ДИЗАЙН-ПРОЕКТ ИНТЕРЬЕРА

# Квартира 58 м²

## *кухня-гостиная и спальня*

**55,23 м²**

светло · спокойно · уютно (hygge) · естественно · функционально · в меру (lagom)

**Палитра из: тёплые нейтрали NCS (стены по ведомости — S 1002-Y50R / S 1502-Y50R близки к ним), акцент — пыльный синий в текстиле.**

ПАЛИТРА 60 / 30 / 10

| NCS S 0500-N | NCS S 1500-N | NCS S 2002-Y | NCS S 4010-R90B |
|---|---|---|---|
| 60 % | 30 % | 30 % | 10 % |


АВТОР ПРОЕКТА

**Кырлан Александр Сергеевич**


Октябрь 2026

место под визуализацию: вид сверху (3D) с мебелью, текстилем и декором

Визуализация «вид сверху» — в работе

| ОБЪЕКТ | ОБЩАЯ ПЛОЩАДЬ | ПОМЕЩЕНИЙ |
|---|---|---|
| Квартира 58 м² | 55,23 м² | 6, из них жилых 2 |
| **СТИЛЬ** | **СТАДИЯ** | **ШИФР** |
| Скандинавский · кухня-гостиная и спальня | Рабочий проект | ГД-2026-006-АИ |

| | | | | | | | |
|---|---|---|---|---|---|---|---|
| | | | | | Проект: Квартира 58 м² | | |
| | Лист | № док. | Подпись | Дата | Титульный лист | Стадия | Лист | Листов |
| Дизайнер | Кырлан А.С. | | | 09.10.26 | | П | 1 | 60 |


выпуск 09.10.2026 · 6e771c53bc · стр. 1 из 60

## Список листов

| Лист | Наименование |
|---|---|
| 1 | Титульный лист |
| 2 | Список листов |
| 3 | План планировки от заказчика |
| 4 | План монтажный |
| 5 | Кухня (пом. 1). Монтажная схема |
| 6 | Шкафы. Монтажная схема |
| 7 | Карта покрытий стен |
| 8 | Колерная карта |
| 9 | План размещения мебели и оборудования |
| 10 | Спецификация мебели и оборудования |
| 11 | Ведомости изделий, техники и фурнитуры |
| 12 | План выводов сантехники |
| 13 | Схема разводки водопровода и канализации |
| 14 | Спецификация сантехнического оборудования |
| 15 | План размещения дверей |
| 16 | План потолков |
| 17 | План розеток и электровыводов |
| 18 | План слаботочных сетей |
| 19 | План освещения |
| 20 | Спецификация светильников и сценарии освещения |
| 21 | Управление светильниками |
| 22 | План вентиляции |
| 23 | План отопления |
| 24 | План покрытий пола |
| 25 | Раскладка плитки. Планы полов |
| 26 | Раскладка плитки. Ванная. Санузел. Прихожая |
| 27 | Визуализация кухни-гостиной |
| 28 | Визуализация кухни-гостиной |
| 29 | Визуализация кухни-гостиной |
| 30 | Развёртка стены В. Кухня-гостиная (пом. 1), кухонный фронт |
| 31 | Развёртка стены А. Кухня-гостиная (пом. 1) |
| 32 | Развёртка стены Б. Кухня-гостиная (пом. 1) |
| 33 | Развёртка стены Г. Кухня-гостиная (пом. 1) |
| 34 | Визуализация спальни |
| 35 | Визуализация спальни |
| 36 | Развёртка стены А. Спальня (пом. 2) |
| 37 | Развёртка стены Б. Спальня (пом. 2) |
| 38 | Развёртка стены В. Спальня (пом. 2) |
| 39 | Визуализация ванной |
| 40 | Визуализация ванной |


| Лист | Наименование |
|---|---|
| 41 | Развёртки стен А, Б. Ванная (пом. 3) |
| 42 | Развёртки стен В, Г. Ванная (пом. 3) |
| 43 | Визуализация санузла |
| 44 | Развёртки стен А, Б. Санузел (пом. 4) |
| 45 | Развёртки стен В, Г. Санузел (пом. 4) |
| 46 | Визуализация прихожей |
| 47 | Визуализация прихожей |
| 48 | Развёртка стены А. Прихожая (пом. 5) |
| 49 | Развёртка стены Б. Прихожая (пом. 5) |
| 50 | Развёртка стены В. Прихожая (пом. 5) |
| 51 | Развёртка стены Г. Прихожая (пом. 5) |
| 52 | Визуализация гардеробной |
| 53 | Развёртки стен А, Б. Гардеробная (пом. 6) |
| 54 | Развёртка стены Г. Гардеробная (пом. 6) |
| Д_1 | Шкаф-купе М_13 |
| Д_2 | Система хранения М_14 |
| Д_3 | Кухня (пом. 1). Развёртка гарнитура |
| С1 | Ведомость отделки помещений |
| С2 | Спецификация отделочных материалов |
| С3 | Узлы |

## Общие указания

1. Размеры даны в мм от чистовых поверхностей стен: слой штукатурки 20 мм по блоку и 5 мм шпаклёвки по ГКЛ учтён. Перед заказом встроенной мебели — контрольный обмер после штукатурки.
2. Привязки мебели — от стен и углов помещения, а не от другой мебели.
3. Розетки, выводы и выключатели под мебель — см. лист 17 «План розеток и электровыводов»; сантехприборы и выводы воды — лист 12.
4. План расстановки не является документацией для изготовления мебели: изделия — по чертежам мебельщика; покупную мебель заменять только на изделия не больше габарита из спецификации (лист 10).
5. Встроенная мебель «стена в стену» — с зазором 10 мм с каждой стороны или с компенсаторами.
6. Развёртки — вид на стену изнутри помещения, по часовой стрелке; расположение стен на схеме листа развёртки; размеры — в мм по чистовым поверхностям; отметки — в м от ±0,000; высоты Н — от чистого пола помещения до оси изделия, у декора — до центра.
7. Красные цепочки — привязки электроточек и выводов: по горизонтали от угла чистовых стен, по вертикали от чистого пола, до оси изделия; звенья короче 3 мм на листе вынесены во второй ярус (ближняя к стене цепочка).
8. У знака электроточки: марка (Р — розетка, S — выключатель, Св — светильник, ЭВ вывод кабеля), *N — число постов в рамке, гр. — группа щита, Н — высота оси от чистого пола, мм; группы по клавишам выключателя — на листе выключателей.
9. Схема мебели, приборов и декора не является технической документацией для производства мебели; габариты — по паспортам изделий.
10. Марки позиций: М_NN — мебель, ОБ_NN — оборудование, С_NN — сантехника; О-N отделка (ведомость отделочных материалов, серия С).
11. Размеры мебели и изделий на заказ уточнить по месту после отделочных работ.

| | | | | | |
|---|---|---|---|---|---|
| | | | | | Проект: Квартира 58 м² |
| | Лист | № док. | Подпись | Дата | |
| Дизайнер | Кырпан А.С. | | | 09.10.26 | Список листов |
| | | | | | Стадия: П; Лист: 2; Листов: 60 |

выпуск 09.10.2026 № 6e771c53bc · стр. 2 из 60

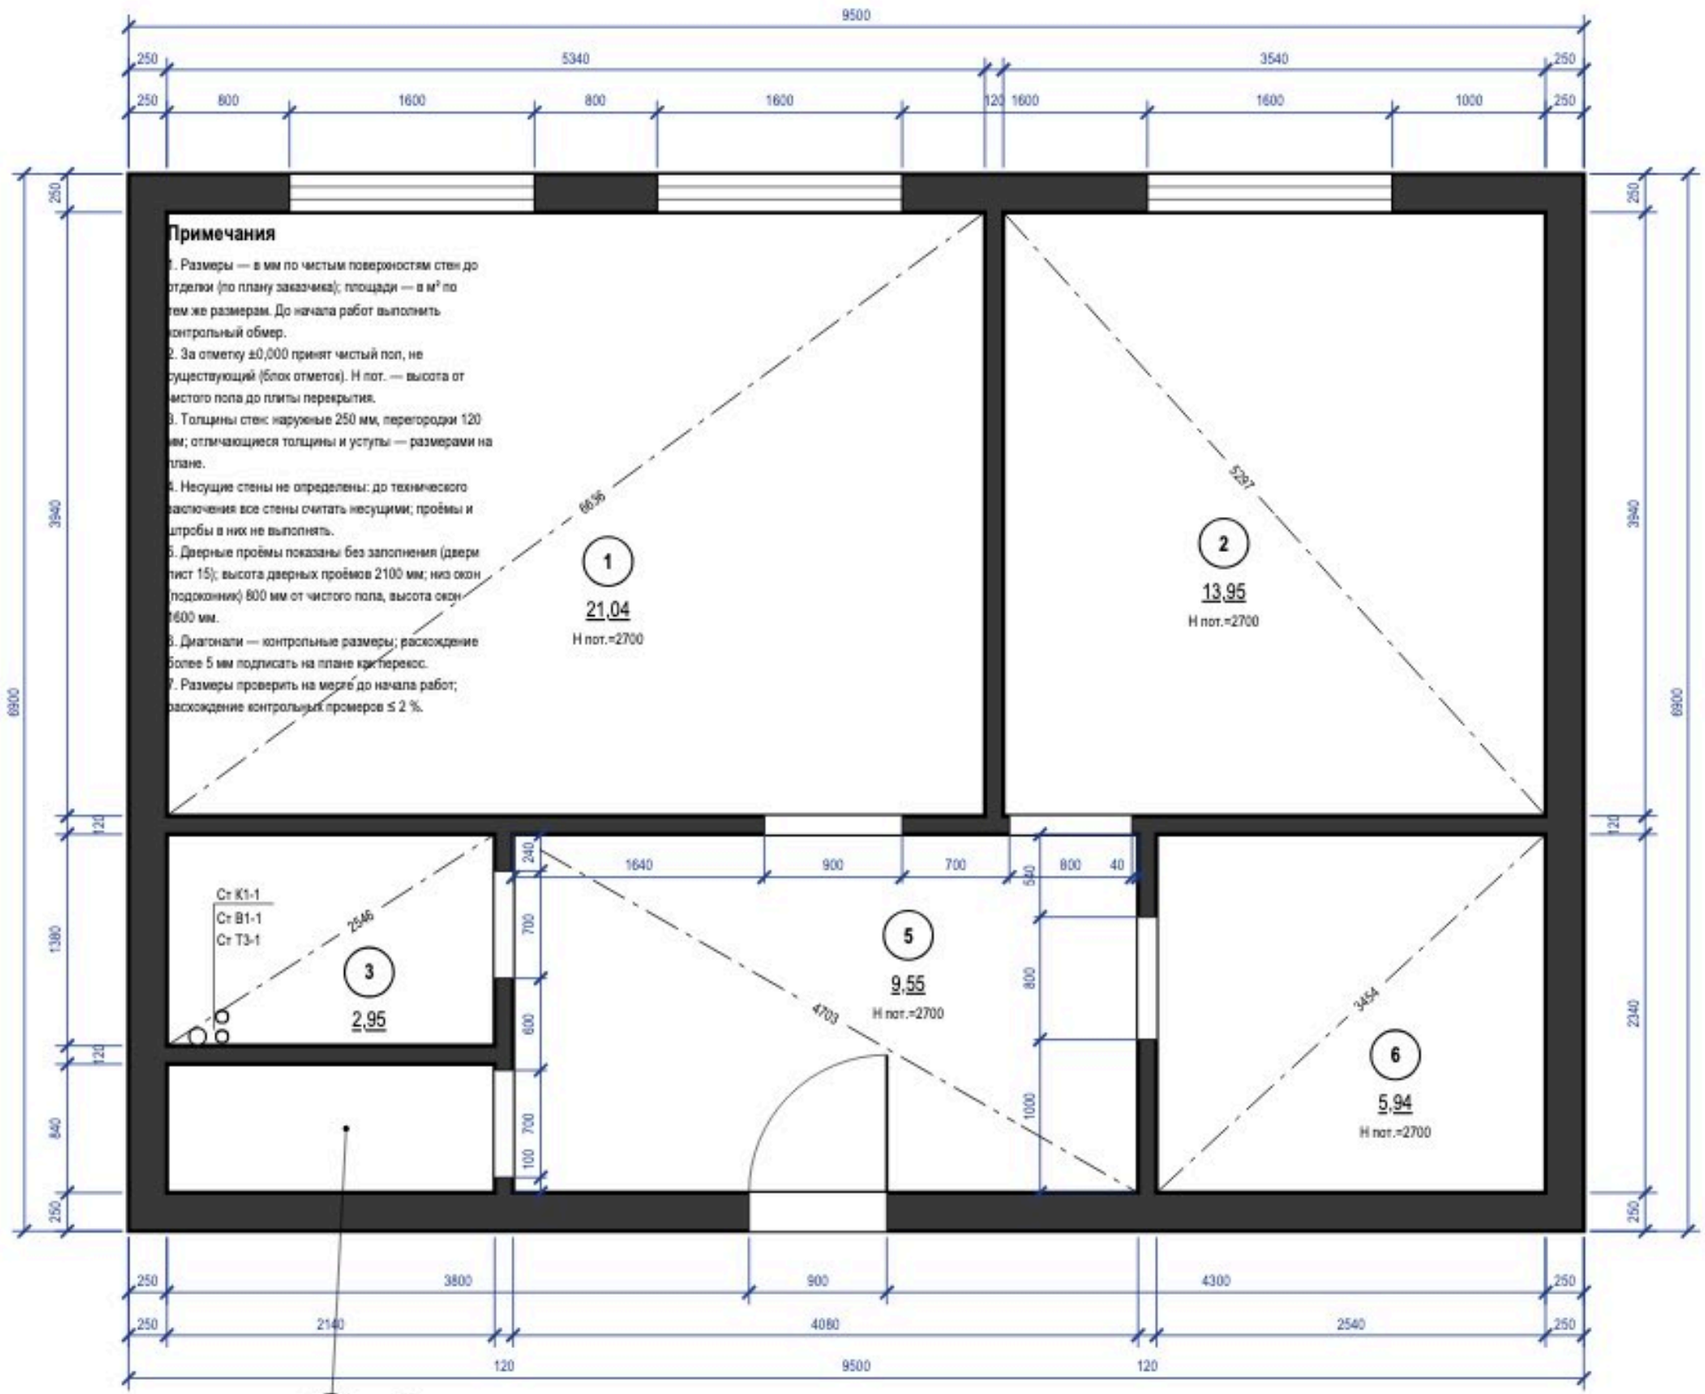


### Отметки по высоте

| | |
|---|---|
| **±0,000** | чистый пол пом. 1, 2, 5, 6; отсчёт высот |
| **−0,015** | чистый пол пом. 3, 4, ниже на 15 мм |
| **−0,064** | верх плиты — расчёт, не замер (задание на обмер) |
| **сущ. пол** | снимается до плиты; не замерен (задание на обмер) |

### Экспликация помещений

| № | Наименование | Площадь, м² |
|---|---|---|
| 1 | Кухня-гостиная | 21,04 |
| 2 | Спальня | 13,95 |
| 3 | Ванная | 2,95 |
| 4 | Санузел | 1,80 |
| 5 | Прихожая | 9,55 |
| 6 | Гардеробная | 5,94 |
| | **Итого (общая площадь)** | **55,23** |


### Условные обозначения

- существующие стены (сечение)
- окно (рама, остекление)
- проём существующий, без заполнения (откосы)
- стояк К1 — канализация, В1 — ХВС, Т3 — ГВС
- диагональ помещения — контроль прямоугольности
- (1) номер помещения, площадь м²

| | | | | | |
|---|---|---|---|---|---|
| | Лист | № док. | Подпись | Дата | Проект: Квартира 58 м² |
| Дизайнер | Кырпан А.С. | | | 09.10.26 | План планировки от заказчика |

| Стадия | Лист | Листов |
|---|---|---|
| П | 3 | 60 |

выпуск 09.10.2026 № 6e771c53bc · стр. 3 из 60

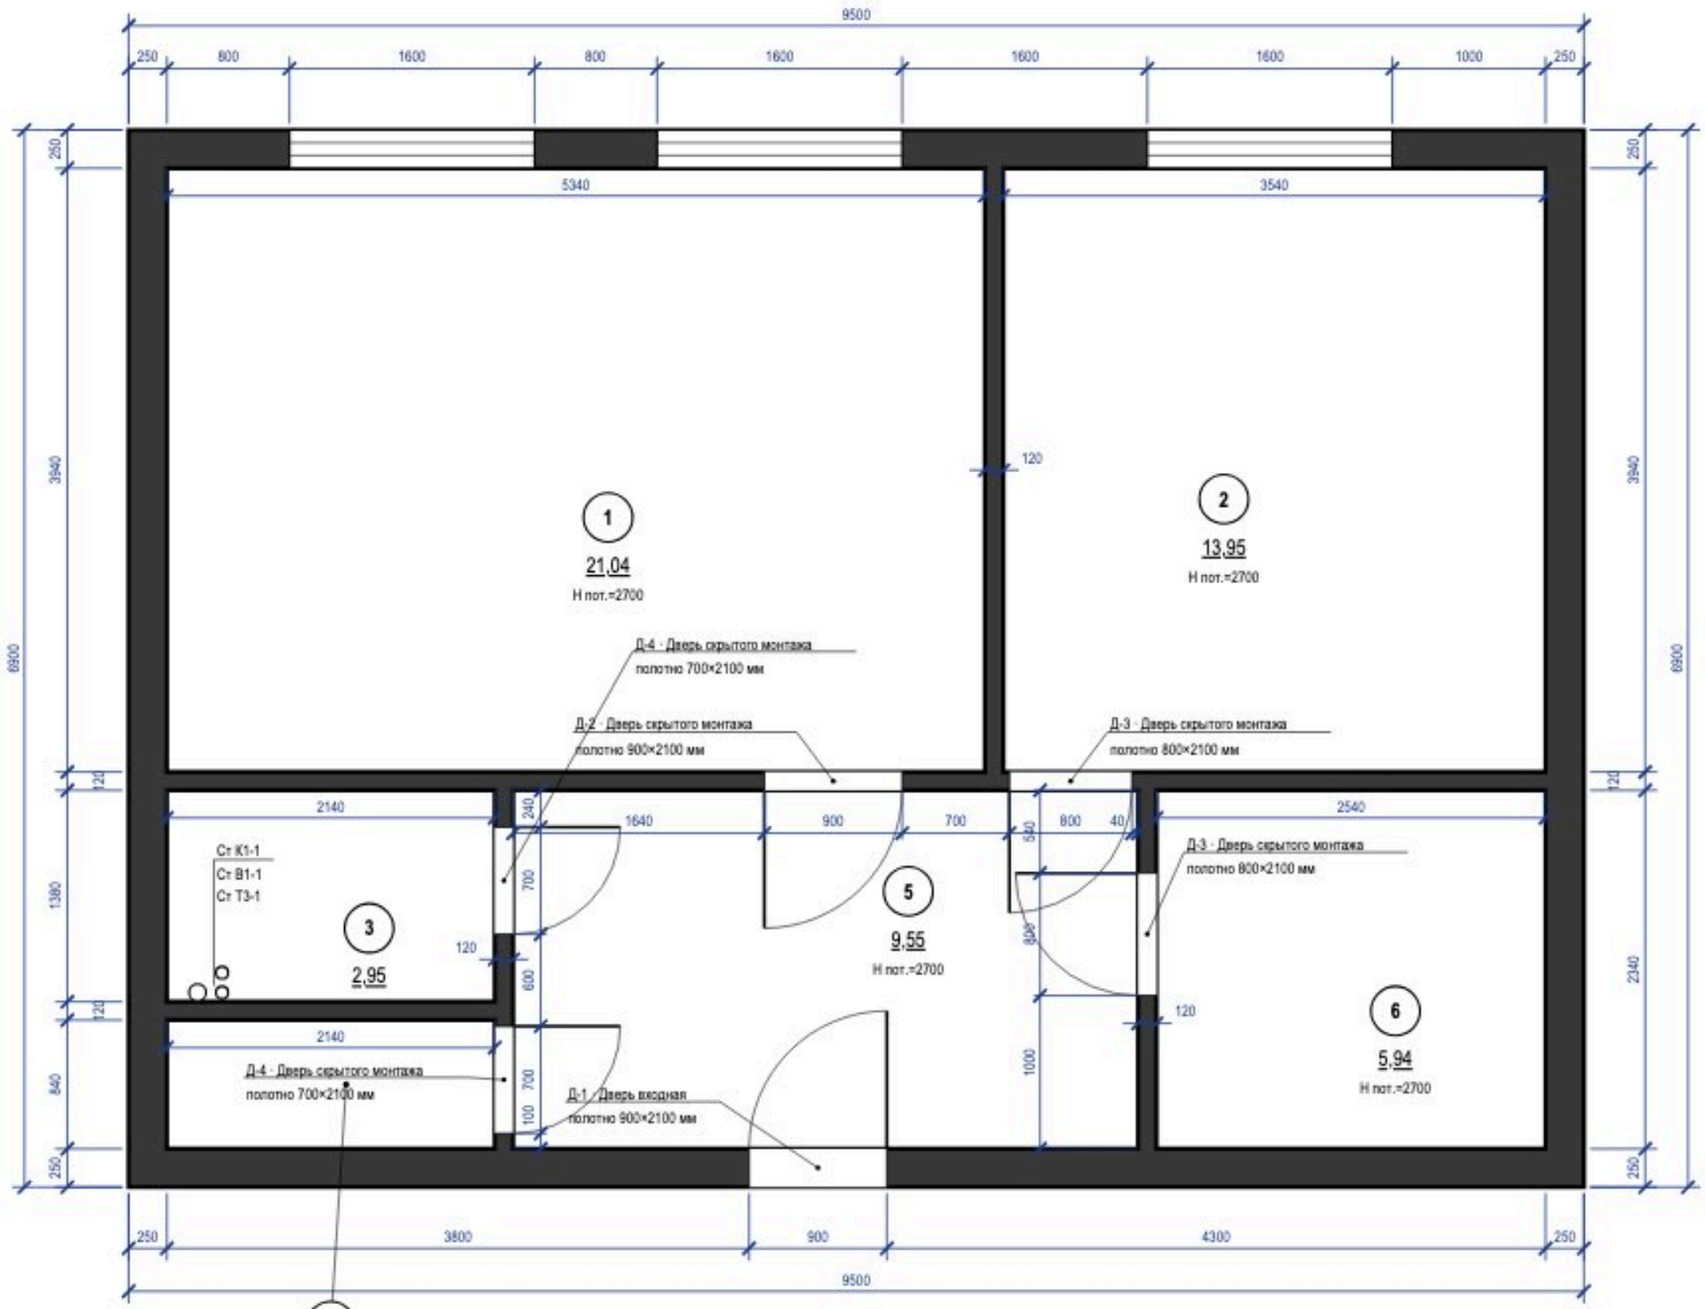


4

1,80

Н пот.=2700

**Экспликация помещений**

| № | Наименование | Площадь, м² |
|---|---|---|
| 1 | Кухня-гостиная | 21,04 |
| 2 | Спальня | 13,95 |
| 3 | Ванная | 2,95 |
| 4 | Санузел | 1,80 |
| 5 | Прихожая | 9,55 |
| 6 | Гардеробная | 5,94 |
| | **Итого (общая площадь)** | **55,23** |

**Примечания**


1. Размеры — в мм от чистовых поверхностей стен до отделки; размеры уточнить по месту до начала работ.
2. Новые перегородки и облицовки — синим; каркас и обшивка — по выноскам; двери и проёмы лист 15.
3. Несущие стены не изменять: проёмы, ниши и штробы в них — только по техническому заключению.

| | | | | | |
|---|---|---|---|---|---|
| | Лист | № док. | Подпись | Дата | Проект: Квартира 58 м² |
| Дизайнер | Кырпан А.С. | | | 09.10.26 | План монтажный |


| Стадия | Лист | Листов |
|---|---|---|
| П | 4 | 60 |

выпуск 09.10.2026 № 6e771c53bc · стр. 4 из 60

## Привязка выводов и крепление модулей

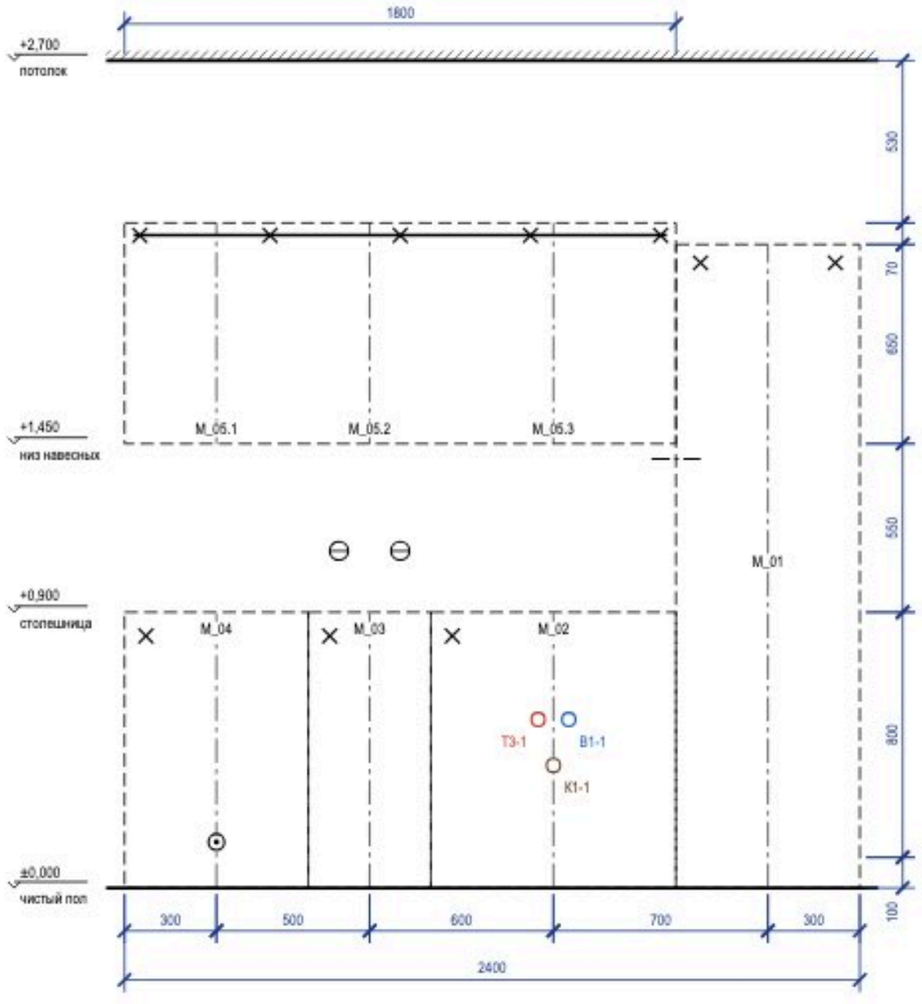


## План столешницы

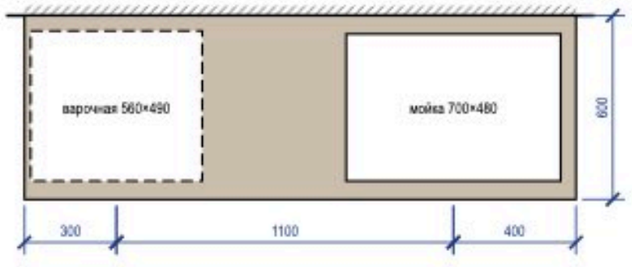


## Привязка выводов к осям модулей

| Код | Назначение | Модуль | От оси, мм | H, мм | Размещение |
|---|---|---|---|---|---|
| | вывод кабеля — варочная панель | M_04 | 0 | 150 | в соседнем модуле, за ящиком |
| | розетка — рабочая зона | M_03 | −100 | 1100 | над столешницей (фартук) |
| | розетка ×2 — рабочая зона | M_03 | +100 | 1100 | над столешницей (фартук) |
| T3-1 | T3 — межос. 100 | M_02 | −50 | 550 | в модуле мойки |
| K1-1 | K1 Ø50 — мойка | M_02 | 0 | 400 | в модуле мойки |
| B1-1 | B1 — межос. 100 | M_02 | +50 | 550 | в модуле мойки |
| | светодиодная лента — подсветка столешницы | M_01 | −300 | 1400 | за пеналом |

## Зазоры под отделку

| Поверхность | Отделка | Зазор, мм | Учесть |
|---|---|---|---|
| фартук | плитка / стеновая панель | 10 | от чернового основания до корпуса навесных и столешницы |
| стены | окраска | 5 | под штукатурку и шпаклёвку за пеналом |
| пол | инженерная доска | | цоколь — после укладки пола, опоры ±20 мм |

## Условные обозначения

- навесной модуль (невидимый контур)
- ось модуля (от неё — привязка вывода)
- анкер / уголок крепления к стене
- розетка на стене
- вывод кабеля к технике
- B1 — вывод воды B1 / T3, канализации K1

## Примечания


1. Выводы — по проекту электрики и ВК; привязка по горизонтали — от оси модуля (плюс — вправо по виду), по высоте — от чистого пола до оси вывода.
2. Пенал — уголки к стене 2 шт. сверху; нижние модули — стяжками между собой и уголком к стене; ряд выставить по уровню опорами цоколя.
3. Розетки над столешницей — не ниже 150 мм над ней и не за корпусом техники; розетка за ПММ, духовым шкафом и холодильником — только в соседнем модуле или в зоне цоколя с доступом.
4. Столешница — вырезы по шаблонам выбранных моделей мойки и варочной панели; торцы у стены — герметик, пристеночный плинтус.

| | | | | | |
|---|---|---|---|---|---|
| | | | | | Проект: Квартира 58 м² |
| | Лист | № док. | Подпись | Дата | Кухня (пом. 1). Монтажная схема |
| Дизайнер | Кырпан А.С. | | | 09.10.26 | |


| Стадия | Лист | Листов |
|---|---|---|
| П | 5 | 60 |

выпуск 09.10.2026 · 6e771c53bc · стр. 5 из 60

### Шкаф-купе М_13 (пом. 5)

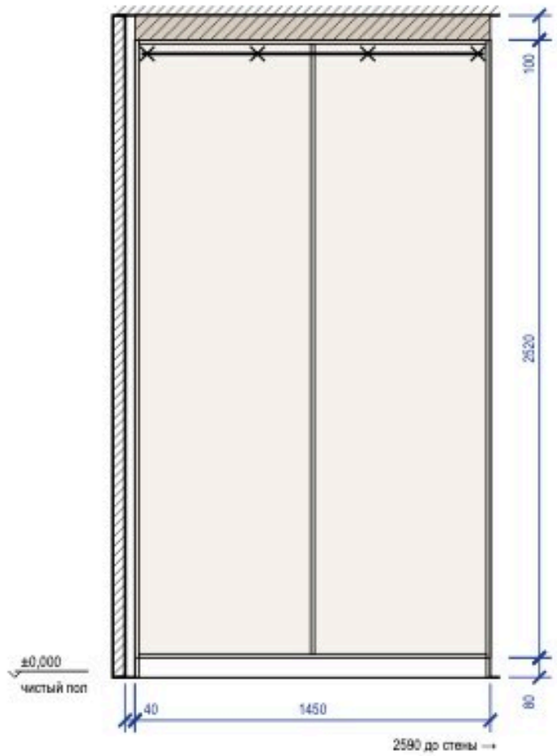


### Система хранения М_14 (пом. 6)

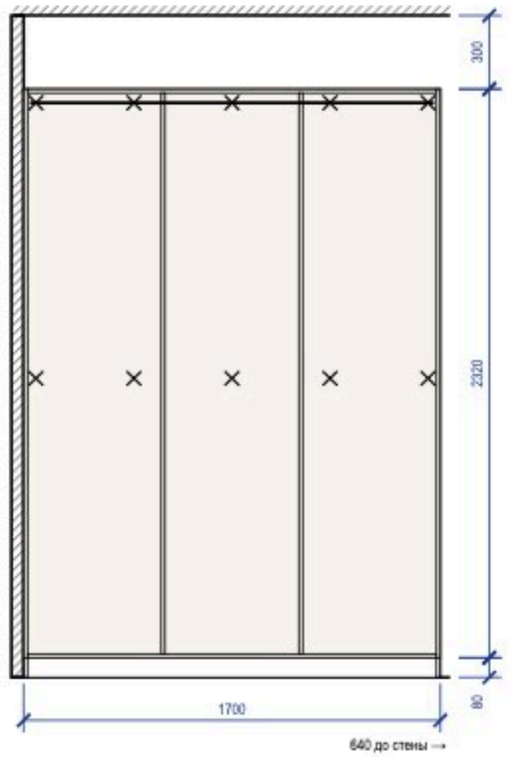


## Крепление и зазоры под отделку

| Марка | Помещение, стена | Основание | Отделка стены | Зазор, мм | Крепёж по плане | От опрокидывания |
|---|---|---|---|---|---|---|
| М_13 | Прихожая (5), стена В | по основанию — см. таблицу крепежа | окраска | 5 | анкер 4 шт., шаг 450 | уголки 2 шт. |
| М_14 | Гардеробная (6), стена Б | по основанию — см. таблицу крепежа | окраска | 5 | анкер 10 шт. (2 ряда) | крепление к стене, 3 точки |

## Крепёж по основанию стены

| Основание стены | Крепёж |
|---|---|
| бетон, ж/б | анкер-шуруп 7,5×72 или дюбель 8×60 с шурупом 5×70 |
| кирпич полнотелый | дюбель 8×80 с шурупом 5×90 |
| газобетон, пазогребень | дюбель для газобетона 10×100 или химический анкер |
| гипсокартон | закладная до обшивки (брус 40×80 или фанера 18 мм), саморез в закладную |

## Условные обозначения


- × — анкер / уголок крепления к стене
- ▭ — корпус и полки ЛДСП (вид на стену)
- ▨ — компенсатор — короб до потолка

## Примечания

1. Установочные размеры — от чистого пола и чистых стен; перед установкой контрольный замер после отделки.
2. Порядок: корпус выставить по уровню опорами цоколя → закрепить к стене по задней планке → навесить двери и фасады, отрегулировать зазоры → подогнать и закрепить компенсатор.
3. Анкеры — с шагом не более 500 мм, не ближе 50 мм от края планки; на ГКЛ только в закладную, установленную до обшивки.
4. Скрытые коммуникации под анкеры проверить детектором; трассы электрики по плану розеток.

| | | | | | Проект: Квартира 58 м² | | | |
|---|---|---|---|---|---|---|---|---|
| | Лист | № док. | Подпись | Дата | Шкафы. Монтажная схема | Стадия | Лист | Листов |
| Дизайнер | Кырпан А.С. | | | 09.10.26 | | П | 6 | 60 |

выпуск 09.10.2026 № 6e771c53bc · стр. 6 из 60

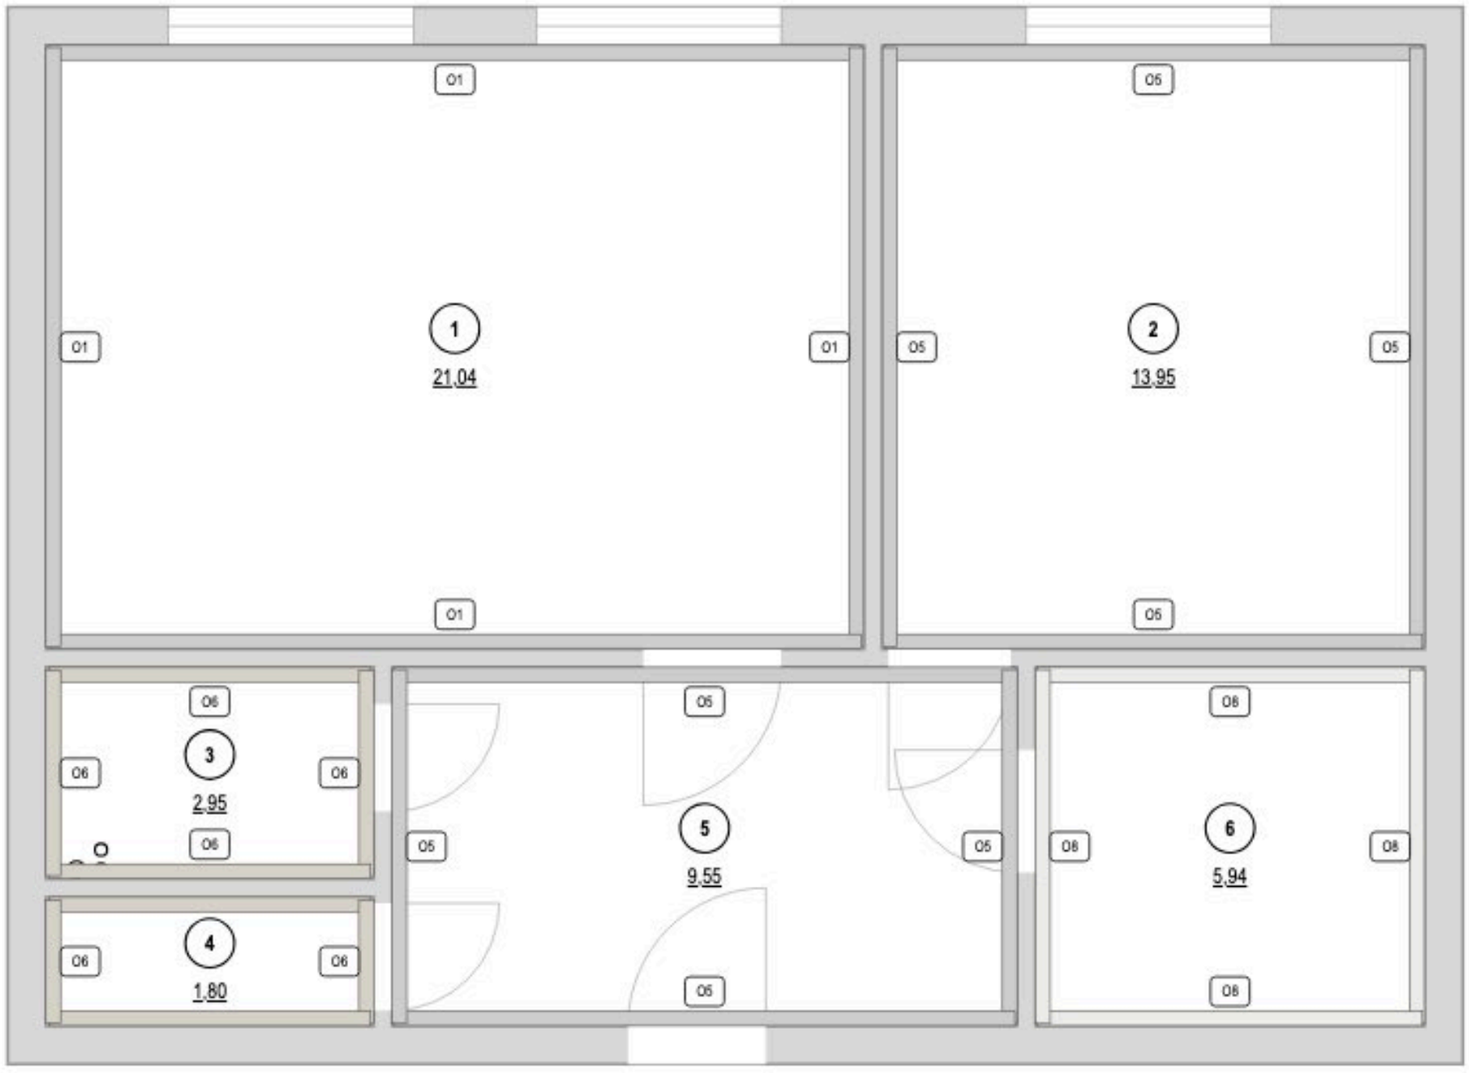


**Покрытия стен**

| Марка | Покрытие | Помещение: S, м² | Итого, м² |
|---|---|---|---|
| О1 | окраска Tikkurila · S 1002-Y50R | 1: 42,8 | 42,8 |
| О5 | окраска Tikkurila · S 1502-Y50R | 2: 35,8; 5: 24,3 | 60,1 |
| О6 | облицовка плиткой Italon · 610015000370 «Charme Extra» 600×1200 мм | 3: 17,2; 4: 14,3 | 31,5 |
| О8 | окраска Tikkurila · V503 «Winter» | 6: 24,3 | 24,3 |

Площади — нетто, по развёрткам (за вычетом проёмов и фартука); высоты помещений — от чистого пола.

| | | | | | |
|---|---|---|---|---|---|
| | | | | | Проект: Квартира 58 м² |
| | Лист | № док. | Подпись | Дата | Карта покрытий стен |
| Дизайнер | Кырпан А.С. | | | 09.10.26 | |

| Стадия | Лист | Листов |
|---|---|---|
| П | 7 | 60 |

выпуск 09.10.2026 · 6e771c53bc · стр. 7 из 60

## Колерная карта по помещениям

| Помещение | Поверхность | Образец | Поз. | Система и код цвета | Производитель, линейка / материал, артикул | Блеск | Класс EN 13300 | LRV | Площадь |
|---|---|---|---|---|---|---|---|---|---|
| **1. Кухня-гостиная** 21,04 м² | стены | | **K1** | NCS S 1002-Y50R | Tikkurila | полуматов. | 1 | 82 | 43,1 м² |
| | потолок | | **K2** | NCS S 0300-N | Tikkurila | глубокомат. | 1 | 92 | 21,0 м² |
| | пол | | **KM1** | по образцу | Quick-Step · Impressive | | | | 21,0 м² |
| | плинтус | | **K3** | NCS S 0300-N | Orac Decor · Luxxus | полуматов. | | 92 | 17,7 м |
| **2. Спальня** 13,95 м² | стены | | **K4** | NCS S 1502-Y50R | Tikkurila | глубокомат. | 2 | 72 | 36,2 м² |
| | потолок | | **K5** | NCS S 0300-N | Tikkurila | глубокомат. | 2 | 92 | 13,9 м² |
| | пол | | **KM1** | по образцу | Quick-Step · Impressive | | | | 13,9 м² |
| | плинтус | | **K3** | NCS S 0300-N | Orac Decor · Luxxus | полуматов. | | 92 | 14,2 м |
| **3. Ванная** 2,95 м² | стены | | **K6** | Italon 610015000370 | Italon · Charme Extra | | | | 17,6 м² |
| | потолок | | **K2** | NCS S 0300-N | Tikkurila | глубокомат. | 1 | 92 | 3,0 м² |
| | пол | | **K7** | Kerama Marazzi SG651622R | Kerama Marazzi · Две Венеции / Риальто | | | | 3,0 м² |
| **4. Санузел** 1,8 м² | стены | | **K6** | Italon 610015000370 | Italon · Charme Extra | | | | 14,7 м² |
| | потолок | | **K2** | NCS S 0300-N | Tikkurila | глубокомат. | 1 | 92 | 1,8 м² |
| | пол | | **K7** | Kerama Marazzi SG651622R | Kerama Marazzi · Две Венеции / Риальто | | | | 1,8 м² |
| **5. Прихожая** 9,55 м² | стены | | **K8** | NCS S 1502-Y50R | Tikkurila | полуматов. | 1 | 72 | 24,6 м² |
| | потолок | | **K2** | NCS S 0300-N | Tikkurila | глубокомат. | 1 | 92 | 9,6 м² |
| | пол | | **K7** | Kerama Marazzi SG651622R | Kerama Marazzi · Две Венеции / Риальто | | | | 9,6 м² |
| | плинтус | | **K3** | NCS S 0300-N | Orac Decor · Luxxus | полуматов. | | 92 | 8,0 м |
| **6. Гардеробная** 5,94 м² | стены | | **K9** | Tikkurila V503 | Tikkurila · Harmony | матовая | 1 | 86 | 24,7 м² |
| | потолок | | **K10** | Tikkurila V503 | Tikkurila · Anti-Reflex 2 | глубокомат. | 2 | 86 | 5,9 м² |
| | пол | | **KM1** | по образцу | Quick-Step · Impressive | | | | 5,9 м² |
| | плинтус | | **K11** | Tikkurila V503 | Orac Decor · Luxxus | | | 86 | 9,0 м |

## Перечень выкрасов на согласование

| № | Код | Бренд / веер | Пом. / стена | Подложка | Формат | Статус |
|---|---|---|---|---|---|---|
| 1 | S 1002-Y50R | NCS Tikkurila | 1 | ГКЛ, загрунтованный под эту краску | 600×1000 | к выполнению |
| 2 | S 0300-N | NCS Tikkurila | 1, 2, 3, 4, 5 | ГКЛ, загрунтованный под эту краску; МДФ, загрунтованный под эмаль | 600×1000; 300×600 | к выполнению |
| 3 | S 1502-Y50R | NCS Tikkurila | 2, 5 | ГКЛ, загрунтованный под эту краску | 600×1000 | к выполнению |
| 4 | V503 | Tikkurila | 6 | ГКЛ, загрунтованный под эту краску; МДФ, загрунтованный под эмаль | 600×1000; 300×600 | к выполнению |

## Примечания

1. Цвет утверждается только по выкрасу на объекте: формат от А3 до 1000×1000 мм на загрунтованном ГКЛ, в 2 слоя (как на стене), не на белой шпаклёвке; смотреть днём и при свете проекта своего помещения, рядом с образцами пола и фасадов. Подпись на обороте: код, бренд и веер, дата.
2. Колеровка машинная в колеровочном центре бренда; каждый код — за один проход, одной партией на весь объём. Колеровщику передаётся только система и код утверждённого веера; плашки и HEX на листе — ориентир, печать не является эталоном цвета.
3. Класс мокрого истирания — EN 13300 (ISO 11998); блеск — по ГОСТ 31975 (ISO 2813), геометрия 60°. LRV — пересчёт координаты L каталога производителя (Y = (/L*+16)/116)²); «≈» — расчёт по HEX, справочно.
4. Площади поверхностей — тем же способом и с теми же цифрами, что в ведомости отделки (способ счёта — в общих указаниях); объём краски к заказу, фасовка и материалы КМ — в спецификации отделочных материалов.
5. Перечень выкрасов составлен по кодам колерной карты; к основному тону стен добавить на выкрас 2 соседних тона того же веера (светлее и темнее), статус отмечать в графе «Статус» при согласовании.

## Схема квартиры: цвет стен и акценты (б/м)




## Схема палитры проекта

Стиль: Скандинавский · схема: нейтральная

| основной | второстепенный | второстепенный | акцентный |
|---|---|---|---|
| **NCS S 0500-N** | **NCS S 1500-N** | **NCS S 2002-Y** | **NCS S 4010-R90B** |
| нейтральный белый | светлый нейтральный серый | серый камень, тёплый | пыльный синий |
| LRV 85 | LRV 64 | LRV 55 | LRV 27 |
| в отделке не применён | в отделке не применён | в отделке не применён | в отделке не применён |

План 60/30/10




Окраска, факт — по площади стен, акцентов, потолков




окрашено всего 216,1 м²; второстепенный тон несут мебель и текстиль

## Условные обозначения

- **K1** NCS S 1002-Y50R · Tikkurila · полуматов. · кл. 1
- **K2** NCS S 0300-N · Tikkurila · глубокомат. · кл. 1
- **K3** NCS S 0300-N · Orac Decor Luxxus · полуматов.
- **K4** NCS S 1502-Y50R · Tikkurila · глубокомат. · кл. 2
- **K5** NCS S 0300-N · Tikkurila · глубокомат. · кл. 2
- **K6** Italon 610015000370 · Charme Extra · Charme Extra
- **K7** Kerama Marazzi SG651622R · Две Венеции / Риальто · Две Венеции / Риальто
- **K8** NCS S 1502-Y50R · Tikkurila · полуматов. · кл. 1
- **K9** Tikkurila V503 · Winter · Harmony · матовая · кл. 1
- **K10** Tikkurila V503 · Winter · Anti-Reflex 2 · глубокомат. · кл. 2
- **K11** Tikkurila V503 · Winter · Luxxus
- **KM1** инженерная доска · IM1861

дерево (доска, паркет, ламинат) — рисунок досок


HEX не задан — цвет только по коду и вееру

К — позиция окраски (код + продукт + блеск), КМ — позиция материала, тон КМ — по описанию артикула, эталон — образец материала; ≈ LRV — расчёт по HEX, справочно

| | | | | | |
|---|---|---|---|---|---|
| | | | | | Проект: Квартира 58 м² |
| | Лист | № док. | Подпись | Дата | Колерная карта |
| Дизайнер | Кырпан А.С. | | | 09.10.26 | |

| Стадия | Лист | Листов |
|---|---|---|
| П | 8 | 60 |

выпуск 09.10.2026 · 6e771c53bc · стр. 8 из 60

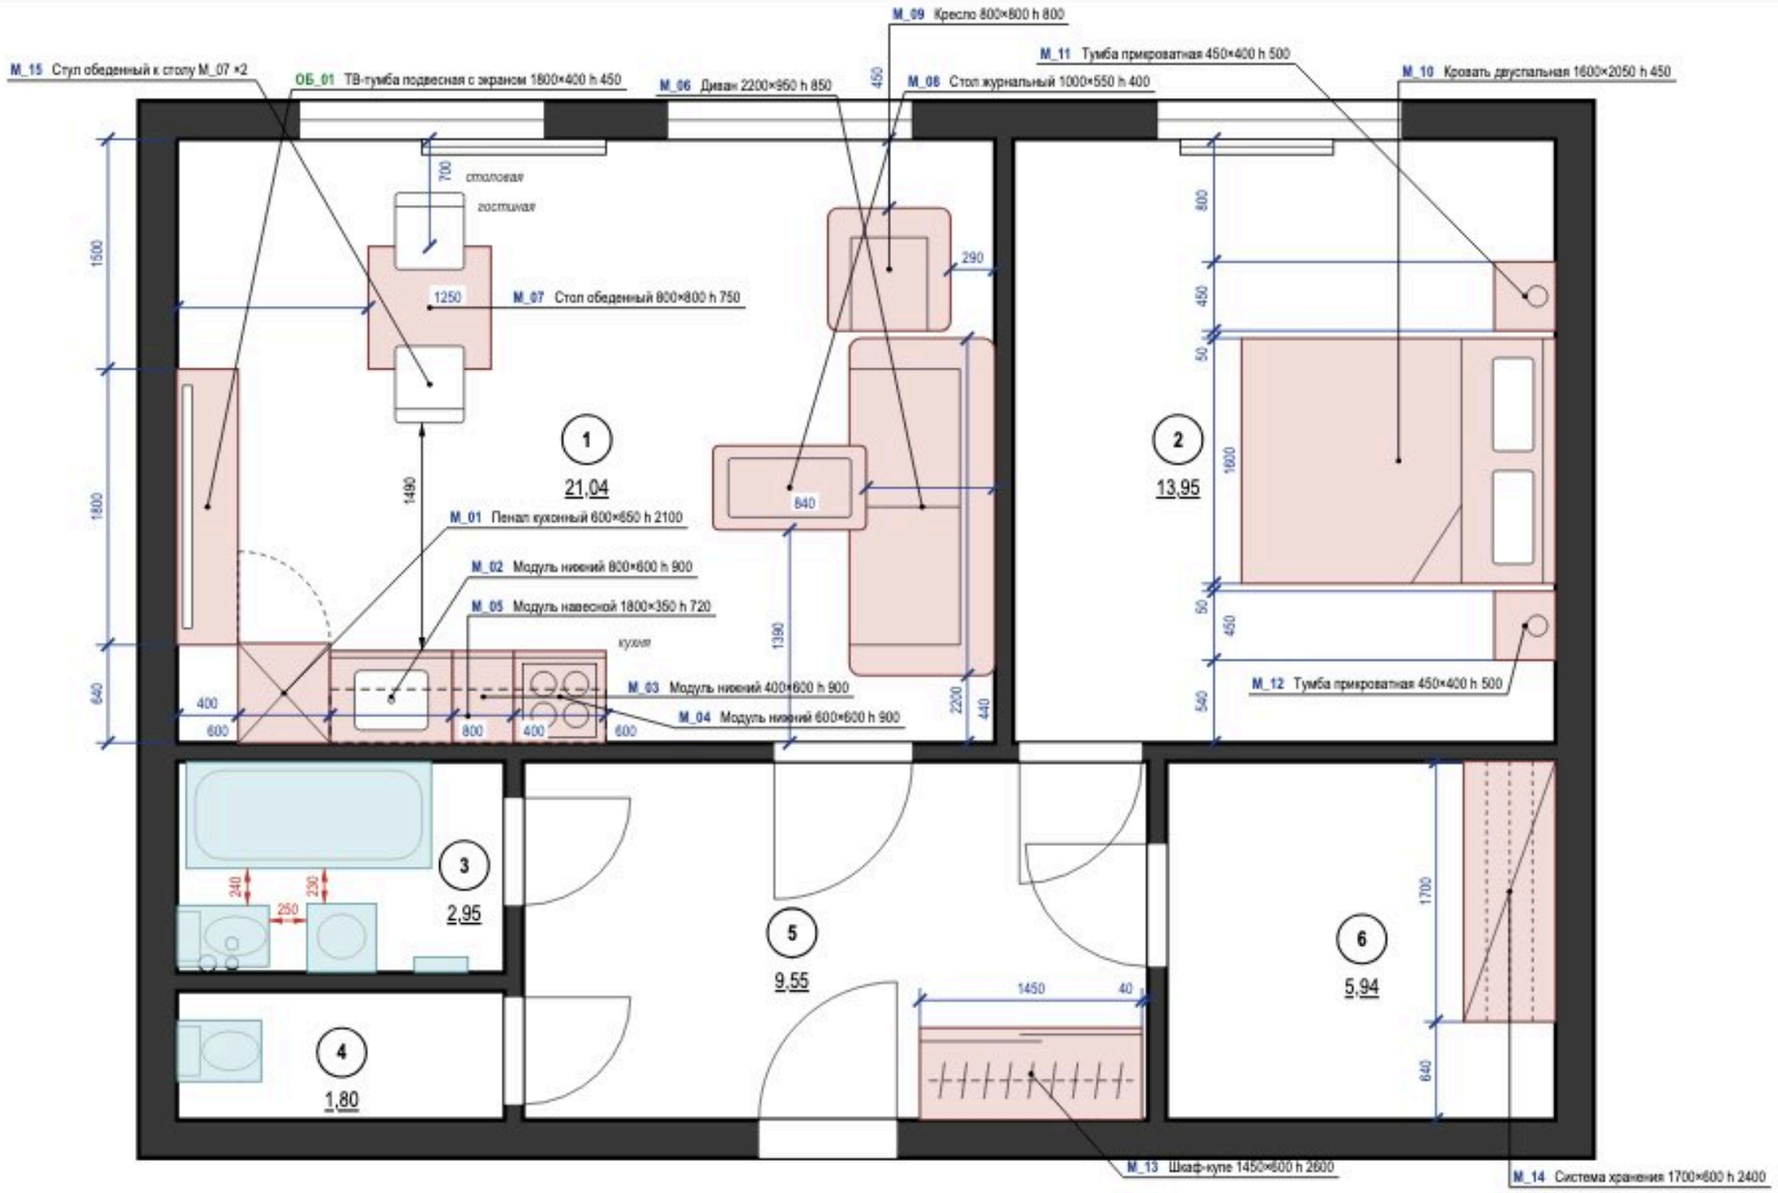


**Экспликация помещений**

лист обмерного плана · на плане — номера в марках

## Ведомость мебели и оборудования

| Марка | Наименование | Ш×Г×В, мм | Пом. | Кол. |
|---|---|---|---|---|
| M_01 | Пенал кухонный | 600×650×2100 | 1 | 1 |
| M_02 | Модуль нижний | 800×600×900 | 1 | 1 |
| M_03 | Модуль нижний | 400×600×900 | 1 | 1 |
| M_04 | Модуль нижний | 600×600×900 | 1 | 1 |
| M_05 | Модуль навесной | 1800×350×720 | 1 | 1 |
| M_06 | Диван | 2200×950×850 | 1 | 1 |
| M_07 | Стол обеденный | 800×800×750 | 1 | 1 |
| ОБ_01 | ТВ-тумба подвесная с экраном | 1800×400×450 | 1 | 1 |
| M_08 | Стол журнальный | 1000×550×400 | 1 | 1 |
| M_09 | Кресло | 800×800×800 | 1 | 1 |
| M_10 | Кровать двуспальная | 1600×2050×450 | 2 | 1 |
| M_11 | Тумба прикроватная | 450×400×500 | 2 | 1 |
| M_12 | Тумба прикроватная | 450×400×500 | 2 | 1 |
| M_13 | Шкаф-купе | 1450×600×2600 | 5 | 1 |
| M_14 | Система хранения | 1700×600×2400 | 6 | 1 |
| M_15 | Стул обеденный к столу M_07 | 450×500×820 | 1 | 2 |

Ш — вдоль стены (изголовья), Г — от стены (длина кровати)

Материалы, модели, допуск замены — лист 10

### Примечания

1. Размеры — в мм от чистовых поверхностей стен; размеры мебели уточнить после отделочных работ; общие указания — лист 2.
2. Стулья обеденной группы (M_15 — 2 шт.) показаны в рабочем положении, задвинутыми под столешницу на 150 мм.

| | | | | | |
|---|---|---|---|---|---|
| | | | | | Проект: Квартира 58 м² |
| | Лист | № док. | Подпись | Дата | План размещения мебели и оборудования |
| Дизайнер | Кырпан А.С. | | | 09.10.26 | |

| Стадия | Лист | Листов |
|---|---|---|
| П | 9 | 60 |

выпуск 09.10.2026 № 6e771c53bc · стр. 9 из 60

| Поз. | Наименование и техническая характеристика | Тип, марка, обозначение документа, опросного листа | Код продукции | Поставщик | Ед. измерения | Кол. | Масса 1 ед., кг | Примечание |
|---|---|---|---|---|---|---|---|---|
| | **Мебель встроенная и корпусная (изготовление по чертежам мебельщика)** | | | | | | | |
| M_01 | Пенал кухонный, холодильник; корпус ЛДСП 16 мм, фасады МДФ эмаль; Ш×Г×В 600×650×2100 мм | | | изготовление на заказ | шт. | 1 | | пом. 1 |
| M_02 | Модуль нижний, мойка; корпус ЛДСП 16 мм, фасады МДФ эмаль; Ш×Г×В 800×600×900 мм | | | изготовление на заказ | шт. | 1 | | пом. 1 |
| M_03 | Модуль нижний; корпус ЛДСП 16 мм, фасады МДФ эмаль; Ш×Г×В 400×600×900 мм | | | изготовление на заказ | шт. | 1 | | пом. 1 |
| M_04 | Модуль нижний, варочная; корпус ЛДСП 16 мм, фасады МДФ эмаль; Ш×Г×В 600×600×900 мм | | | изготовление на заказ | шт. | 1 | | пом. 1 |
| M_05 | Модуль навесной; корпус ЛДСП 16 мм, фасады МДФ эмаль; Ш×Г×В 1800×350×720 мм | | | изготовление на заказ | шт. | 1 | | пом. 1 |
| M_13 | Шкаф-купе; корпус ЛДСП, фасады — матовая эмаль в цвет стен (NCS S 1502-Y50R); Ш×Г×В 1450×600×2600 мм | | | изготовление на заказ | шт. | 1 | | пом. 5 |
| M_14 | Система хранения: штанги, полки, ящики; каркас и полки — ЛДСП, декор «дуб натуральный»; Ш×Г×В 1700×600×2400 мм | | | изготовление на заказ | шт. | 1 | | пом. 6; крепление к стене |
| | **Мебель покупная** | | | | | | | |
| M_06 | Диван; обивка — ткань, цвет NCS S 1500-N; Ш×Г×В 2200×950×850 мм | | | аналог по характеристикам | шт. | 1 | | пом. 1; замена ≤ габарита |
| M_07 | Стол обеденный; шпон, дуб натуральный, матовое масло; Ш×Г×В 800×800×750 мм | | | аналог по характеристикам | шт. | 1 | | пом. 1; замена ≤ габарита |
| M_08 | Стол журнальный; шпон, дуб натуральный, матовое масло; Ш×Г×В 1000×550×400 мм | | | аналог по характеристикам | шт. | 1 | | пом. 1; замена ≤ габарита |
| M_09 | Кресло; обивка — ткань, цвет NCS S 1500-N; Ш×Г×В 800×800×800 мм | | | аналог по характеристикам | шт. | 1 | | пом. 1; замена ≤ габарита |
| M_15 | Стул обеденный к столу M_07; обивка — ткань, цвет NCS S 1500-N; каркас — дуб натуральный; Ш×Г×В 450×500×820 мм | | | аналог по характеристикам | шт. | 2 | | пом. 1; замена ≤ габарита |
| ОБ_01 | ТВ-тумба подвесная с экраном; шпон, дуб натуральный, матовое масло; Ш×Г×В 1800×400×450 мм | | | аналог по характеристикам | шт. | 1 | | пом. 1; замена ≤ габарита |
| M_10 | Кровать двуспальная; мягкое изголовье, обивка — ткань, цвет NCS S 1500-N; Ш×Г×В 1600×2050×450 мм | | | аналог по характеристикам | шт. | 1 | | пом. 2; замена ≤ габарита |
| M_11, M_12 | Тумба прикроватная; шпон, дуб натуральный, матовое масло; Ш×Г×В 450×400×500 мм | | | аналог по характеристикам | шт. | 2 | | пом. 2; замена ≤ габарита |
| | **Техника встраиваемая и бытовая, светильники под розетки** | | | | | | | |
| | Холодильник, в модуле M_01 | | | аналог по характеристикам | шт. | 1 | | пом. 1; по схеме изготовителя |
| | Варочная панель встраиваемая, электрическая, в модуле M_04 | | | аналог по характеристикам | шт. | 1 | | пом. 1; по схеме изготовителя |
| | Торшер, у поз. M_07; абажур — ткань или опаловое стекло; лампа 3000 K | | | аналог по характеристикам | шт. | 1 | | пом. 1; розетка — по плану розеток (ЭОМ) |

## Примечания

1. Позиции мебели совпадают с марками на плане расстановки; размеры Ш×Г×В — Ш вдоль стены, Г от стены.
2. Встроенная и корпусная мебель изготавливается по чертежам мебельщика после контрольного обмера; графы «Тип, марка» и «Код продукции» для неё не заполняются (ГОСТ 21.110-2013).
3. Покупные изделия — аналог по характеристикам: заменять только на изделия не больше указанного габарита и того же материала и цвета.
4. Материал и цвет, не указанные в данных изделия, приняты по концепции: тон дерева — по полу, обивка — по вторичному цвету палитры; образцы согласовать до заказа.
5. Масса 1 ед. для изделий до 25 кг не указывается. Техника — по монтажным схемам изготовителя; выводы — по листам ЭОМ и ВК.

| | | | | | | |
|---|---|---|---|---|---|---|
| | | | | | Проект: Квартира 58 м² | |
| | Лист | № док. | Подпись | Дата | Спецификация мебели и оборудования | Стадия / Лист / Листов |
| Дизайнер | Кырпан А.С. | | | 09.10.26 | | П / 10 / 60 |

выпуск 09.10.2026 № 6e771c53bc · стр. 10 из 60

## Ведомость изделий

| Марка | Наименование | Пом. | Ш×Г×В, мм | Корпус | Фасад | Кромка, мм скр./вид. | Кол. |
|---|---|---|---|---|---|---|---|
| М_13 | Шкаф-купе | 5 | 1450×600×2600 | ЛДСП 16 | рифлёные панели МДФ в алюминиевом профиле | 0,4 / 1 | 1 |
| М_14 | Система хранения | 6 | 1700×600×2400 | ЛДСП 16 | без фасадов; ящики — МДФ 18, эмаль матовая | 0,4 / 2 | 1 |
| М_04 | Модуль нижний: ящики, варочная | 1 | 600×600×900 | ЛДСП 16 | МДФ эмаль | 0,4 / 1 | 1 |
| М_05 | Модуль навесной: полки, сушка | 1 | 1800×350×720 | ЛДСП 16 | МДФ эмаль | 0,4 / 1 | 1 |
| М_03 | Модуль нижний: ящики | 1 | 400×600×900 | ЛДСП 16 | МДФ эмаль | 0,4 / 1 | 1 |
| М_02 | Модуль нижний: мойка | 1 | 800×600×900 | ЛДСП 16 | МДФ эмаль | 0,4 / 1 | 1 |
| М_01 | Пенал: холодильник | 1 | 600×650×2100 | ЛДСП 16 | МДФ эмаль | 0,4 / 1 | 1 |

## Ведомость встраиваемой техники

| Поз. | Прибор | Ниша, вырез, мм | Вентиляция | Питание | Схема |
|---|---|---|---|---|---|
| М_04 | Варочная панель индукционная, 60 см | вырез в столешнице 560 × 490 | | вывод кабеля под модулем | по модели |
| М_02 | Мойка врезная / подстольная с сифоном | вырез по шаблону, ориентир 700 × 480 | | смеситель — выводы ВК | по модели |
| М_01 | Холодильник отдельностоящий | проём 600, зазор сверху ≥ 50 | по паспорту модели | розетка рядом, не за корпусом | по модели |
| М_04 | Вытяжка настенная, 60 см | низ ≥ 650 над панелью | воздуховод к вентканалу, короб до потолка | вывод кабеля в коробе | по модели |

## Ведомость фурнитуры

| № | Фурнитура | Тип, размер | Изделия | Кол. |
|---|---|---|---|---|
| 1 | Система дверей купе: профиль, направляющие, ролики | на 2 двери | М_13 | 1 |
| 2 | Ручка-профиль вертикальная | в цвет профиля | М_13 | 2 |
| 3 | Полкодержатель с фиксацией | ø5 мм | М_13, М_14, М_05 | 64 |
| 4 | Штанга овальная 30×15, L = 701 | + 2 держателя | М_13 | 1 |
| 5 | Полка для обуви выдвижная наклонная | ширина 701 | М_13 | 3 |
| 6 | Опора регулируемая с цоколем на клипсах | ход 20 мм | М_13, М_14 | 14 |
| 7 | Анкер по основанию стены | по таблице крепежа | М_13, М_14, М_05 | 19 |
| 8 | Уголок крепления к стене от опрокидывания | стальной | М_13, М_14, М_01 | 6 |
| 9 | Штанга овальная 30×15, L = 545 | + 2 держателя | М_14 | 3 |
| 10 | Направляющие полного выдвижения с доводчиком NL 500 | пара | М_04, М_03 | 6 |
| 11 | Ручка-профиль | латунь матовая | М_04, М_05, М_03, М_02 | 13 |
| 12 | Опора кухонная регулируемая 100–120 мм | + клипса цоколя | М_04, М_03, М_02, М_01 | 18 |
| 13 | Петля накладная 110° с доводчиком | чашка 35 мм | М_05, М_02 | 14 |
| 14 | Сушка для посуды в шкаф | ширина 800 | М_05 | 1 |
| 15 | Навес регулируемый для навесного шкафа | пара на секцию | М_05 | 3 |
| 16 | Шина монтажная | L = 1740 | М_05 | 1 |

### Примечания


1. Модели техники выбирает заказчик до изготовления мебели; ниши, вырезы и вентиляция — по монтажной схеме выбранной модели (условие гарантии), её номер вносится в ведомость.
2. Количество фурнитуры — по чертежам изделий; запас крепежа 5 %. Аналоги — по характеристикам (доводчик, нагрузка, ход).
3. Цвет корпусов, фасадов и профилей — по колерной карте проекта.

| | | | | | |
|---|---|---|---|---|---|
| | | | | | Проект: Квартира 58 м² |
| | Лист | № док. | Подпись | Дата | Ведомости изделий, техники и фурнитуры |
| Дизайнер | Кырпан А.С. | | | 09.10.26 | |

| Стадия | Лист | Листов |
|---|---|---|
| П | 11 | 60 |

выпуск 09.10.2026 № 6e771c53bc · стр. 11 из 60

## Фрагмент 1. Кухня-гостиная (пом. 1)

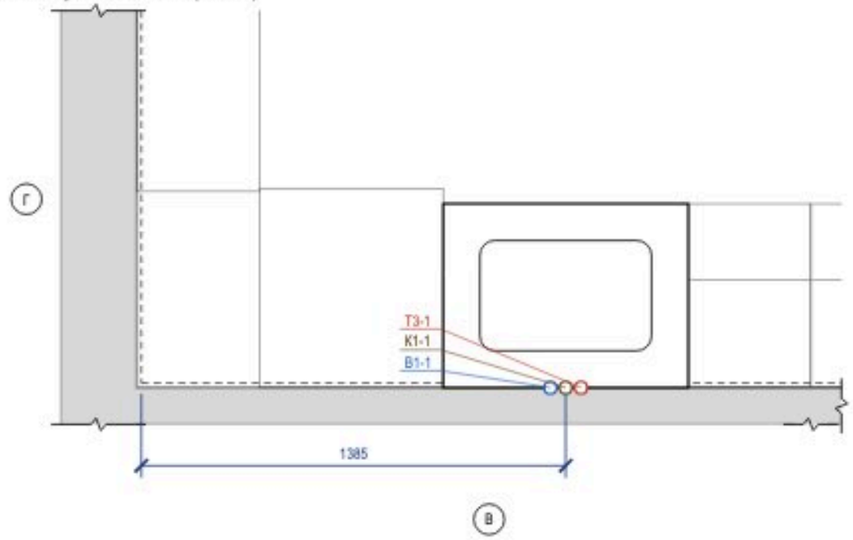



## Ведомость привязок выводов

| Код | Прибор | Ø | H, мм | Привязка от чист. стен, мм | Прим. |
|---|---|---|---|---|---|
| В1-1 | С_01 мойка кухонная | ½" | 550 | ст. В: 1335 от Г | межос. 100 |
| Т3-1 | С_01 мойка кухонная | ½" | 550 | ст. В: 1435 от Г | межос. 100 |
| К1-1 | С_01 мойка кухонная | Ø50 | 400 | ст. В: 1385 от Г | |
| В1-2 | С_02 ванна | ½" | 800 | ст. А: 915 от Г | межос. 150 |
| Т3-2 | С_02 ванна | ½" | 800 | ст. А: 765 от Г | межос. 150 |
| К1-2 | С_02 ванна | Ø50 | 50 | ст. А: 240 от Г | |
| В1-3 | С_03 унитаз подвесной | ½" | 1000 | ст. Г: 370 от В | в раме инсталляции |
| К1-3 | С_03 унитаз подвесной | Ø110 | 220 | ст. Г: 220 от В | |
| В1-4 | С_04 умывальник | ½" | 550 | ст. В: 1005 от Г | межос. 100 |
| Т3-3 | С_04 умывальник | ½" | 550 | ст. В: 995 от Б | межос. 100 |
| К1-4 | С_04 умывальник | Ø50 | 500 | ст. В: 1045 от Б | |
| В1-5 | С_06 унитаз подвесной | ½" | 150 | ст. Г: 220 от А | в раме инсталляции |
| К1-5 | С_06 унитаз подвесной | Ø110 | 230 | ст. Г: 370 от А | |


## Условные обозначения

- вывод В1 (код — в ведомости привязок)
- вывод Т3 (код — в ведомости привязок)
- вывод К1 (код — в ведомости привязок)
- сантехприбор по расстановке (габарит модели)
- чистовая поверхность стены (от неё привязки)
- стояк «Ст К1-N / Ст В1-N» (ГОСТ 21.601), Ø мм
- линия обрыва (граница фрагмента)
- А — обозначение стены А–Г (как на развёртках)

## Фрагмент 2. Ванная (пом. 3)

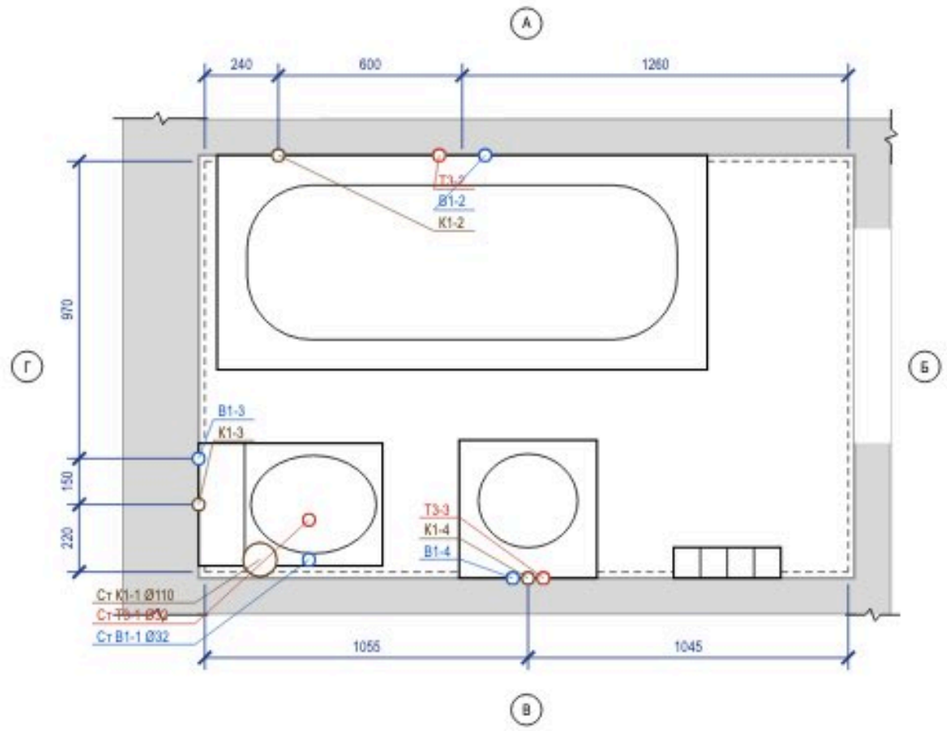


## Фрагмент 3. Санузел (пом. 4)

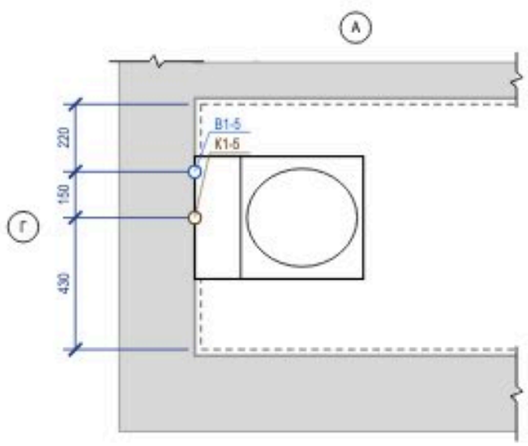



## Примечания

1. Привязки выводов даны от чистовых поверхностей стен (облицовка на сторону: кухня-гостиная — 15 мм (по данным); ванная — 20 мм (по данным); санузел — 20 мм (по данным)); эти же грани — на развёртках и в раскладке плитки. Высоты — от чистого пола помещения.
2. До черновой разводки сверить по паспорту выбранного прибора (смеситель, инсталляция, сифон).
3. Горячая вода (Т3) — слева от холодной (В1), если смотреть на прибор. Допуск установки выводов: ±5 мм в группе, ±20 мм у отдельно стоящих.
4. Расчёт систем водоснабжения и канализации и подбор оборудования выполняет проектная организация; лист задаёт места и высоты выводов.

| | | | | | | | |
|---|---|---|---|---|---|---|---|
| | | | | | Проект: Квартира 58 м² | | |
| | Лист | № док. | Подпись | Дата | План выводов сантехники | Стадия | Лист | Листов |
| Дизайнер | Кырпан А.С. | | | 09.10.26 | | П | 12 | 60 |

выпуск 09.10.2026 · 6e771c53bc · стр. 12 из 60


## План квартиры (М 1:200)

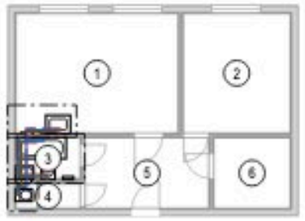



## Фр. 1. Кухня-гостиная (М 1:20)




## Фр. 2. Ванная (М 1:20)

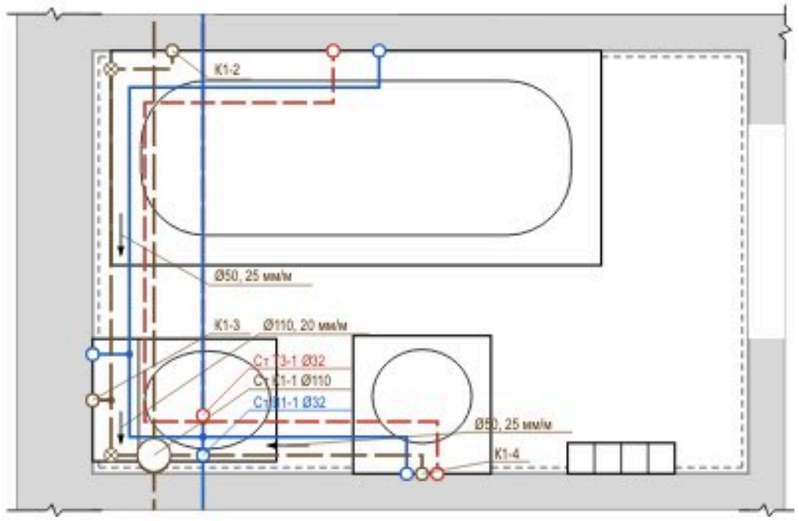


## Фр. 3. Санузел (М 1:20)

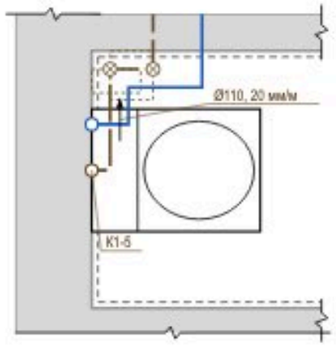


## Условные обозначения

- В1 — водопровод хозяйственно-питьевой (ХВС), PP-R Ø20
- Т3 — горячее водоснабжение, подача (ГВС), PP-R Ø20
- К1 — канализация бытовая
- направление уклона К1 / пола: Ø, мм на 1 м
- ⊗ ревизия (прочистка) К1 — доступ сохранить
- • тройник (ответвление к прибору)
- короб К1 над чистым полом (ГКЛВ под плитку)
- ○ вывод В1 (код — в ведомости привязок)
- ○ вывод Т3 (код — в ведомости привязок)
- ○ вывод К1 (код — в ведомости привязок)
- сантехприбор по расстановке (габарит модели)
- ○ стояк «Ст К1-N / Ст В1-N» (ГОСТ 21.601), Ø мм
- линия обрыва (граница фрагмента)
- граница фрагмента на плане (Фр. N)

## Профиль выпусков К1 (до врезки в стояк)

| Выпуск | Прибор | Ø | L, м | i, мм/м | Δh, мм | Прокладка, мм |
|---|---|---|---|---|---|---|
| К1-5 | С_06 унитаз подвесной | Ø110 | 0,77 | 20 | 15 | короб 160×140 |
| К1-3 | С_03 унитаз подвесной | Ø110 | 0,38 | 20 | 8 | в полу: нужно 193 > 90 — решение! |
| К1-1 | С_01 мойка кухонная | Ø50 | 2,76 | 25 | 69 | короб 150×110 |
| К1-2 | С_02 ванна | Ø50 | 1,68 | 25 | 42 | в полу: нужно 167 > 90 — решение! |
| К1-4 | С_04 умывальник | Ø50 | 0,94 | 25 | 23 | над полом за приборами |

Короб h×b: h — от чистого пола, b — от чистовой стены. Стяжка 90 мм — лист полов.

## Узел ввода В1, Т3 (схема, без масштаба)




⊗ Ст К1-1: ревизия на стояке — люк в коробе

## Примечания

1. Трассы принципиальные, построены от стояков вдоль стен помещений; фактическое положение фиксируется исполнительной схемой с привязками (фото с рулеткой) до закрытия.
2. Уклон К1 не менее 1/d и не более 150 мм/м (СП 30.13330.2020, п. 19.1), приняты практические уклоны; поворот — двумя отводами 45°, ревизия после поворота, доступ сохранить. Стояк К1 в коробе — звукоизоляция стояка в коробе, без жёсткого контакта короба с трубой.
3. Решение по К1: стяжка 90 мм не укрывает трубы (нужно Ø + Δh + 45 мм) — выпуски идут над чистым полом вдоль стен: К1-4 — за приборами и в раме инсталляции; К1-5, К1-1 — в коробе ГКЛВ под плитку (размеры в профиле). Короба — на развёртках; отметку низа врезки в стояк замерить до черновых работ.
4. На каждом вводе В1 и Т3 — кран шаровой, фильтр, счётчик, обратный клапан; доступ через люк не меньше 300×400. Водопровод — в штробе стен или в коробах; трубы испытать давлением до закрытия (акт скрытых работ).
5. Расчёт систем, диаметры магистралей и подбор оборудования выполняет проектная организация; врезка и перенос стояков — по согласованию с управляющей организацией. Арматуру и привязки сверить по паспортам приборов.

| | | | | | |
|---|---|---|---|---|---|
| | | | | | Проект: Квартира 58 м² |
| | Лист | № док. | Подпись | Дата | Схема разводки водопровода и канализации |
| Дизайнер | Кырпан А.С. | | | 09.10.26 | |

| Стадия | Лист | Листов |
|---|---|---|
| П | 13 | 60 |

выпуск 09.10.2026 · 6e771c53bc · стр. 13 из 60

| Поз. | Наименование и техническая характеристика | Тип, марка, обозначение документа | Код продукции | Поставщик | Ед. изм. | Кол. | Масса 1 ед., кг | Примечание |
|---|---|---|---|---|---|---|---|---|
| | Санитарные приборы | | | | | | | |
| 1 | Ванна акриловая 1600×700 мм, с каркасом, экраном и отверстием слив-перелив | Roca Easy ZRU9302899 | | выбор заказчика | шт | 1 | | С_02 |
| 2 | Унитаз подвесной безободковый, с сиденьем микролифт, крепёж и звукоизолирующая прокладка | Laufen Pro 8.2096.6.000.000.1 | | выбор заказчика | шт | 2 | | С_03, С_06 |
| 3 | Инсталляция для подвесного унитаза: рама высотой 1120 мм, бачок, клавиша смыва (ось клавиши 1050 мм от чистого пола) | аналог | | выбор заказчика | шт | 2 | | С_03, С_06; короб ГКЛВ |
| 4 | Умывальник подвесной 450×450 мм, с отверстием под смеситель и переливом | Laufen Pro S 8.1096.3.000.104.1 | | выбор заказчика | шт | 1 | | С_04 |
| 5 | Мойка кухонная 800×600 мм, с переливом | мойка врезная 780×510 в шкафу М_02 | | с кухонной мебелью | шт | 1 | | С_01 |
| 6 | Полотенцесушитель электрический, IP44, с терморегулятором | аналог | | выбор заказчика | шт | 1 | | С_05 |
| | Смесители, сифоны и арматура приборов | | | | | | | |
| 7 | Смеситель для ванны настенный однорычажный, межосевое 150 мм, с душевым набором (лейка, шланг, держатель) | аналог | | выбор заказчика | шт | 1 | | С_02 |
| 8 | Смеситель для умывальника однорычажный, с донным клапаном | аналог | | выбор заказчика | шт | 1 | | С_04 |
| 9 | Смеситель кухонный однорычажный, высокий излив | аналог | | выбор заказчика | шт | 1 | | С_01 |
| 10 | Обвязка ванны слив-перелив Ø40/50 с сифоном | аналог | | выбор заказчика | шт | 1 | | С_02 |
| 11 | Сифон для умывальника бутылочный Ø32/40–50, с гофрой к выпуску | аналог | | выбор заказчика | шт | 1 | | С_04 |
| 12 | Сифон для мойки Ø40/50 | аналог | | выбор заказчика | шт | 1 | | С_01 |
| 13 | Кран угловой ½"×½" с гибкой подводкой 40 см (умывальники, мойка) | аналог | | выбор заказчика | шт | 4 | | по 2 на прибор |
| | Трубопроводы | | | | | | | |
| 14 | Труба полипропиленовая PP-R PN20 Ø20×3,4 (В1) | ГОСТ 32415-2013 | | выбор заказчика | м | 11 | 0,17 | 6,7 + 3,0 + 10 % |
| 15 | Труба PP-R, армированная стекловолокном, PN20 Ø20×2,8 (Т3) | ГОСТ 32415-2013 | | выбор заказчика | м | 8,5 | 0,15 | 5,7 + 1,9 + 10 % |
| 16 | Труба канализационная ПП Ø50 (К1) | ГОСТ 32414-2013 | | выбор заказчика | м | 7 | | 5,0 + 0,9 + 10 % |
| 17 | Труба канализационная ПП Ø110 (К1) | ГОСТ 32414-2013 | | выбор заказчика | м | 2 | | 1,1 + 0,5 + 10 % |
| | Фасонные части и выводы | | | | | | | |
| 18 | Отвод канализационный ПП 45° Ø50 | ГОСТ 32414-2013 | | выбор заказчика | шт | 10 | | 2 шт. на поворот |
| 19 | Отвод канализационный ПП 45° Ø110 | ГОСТ 32414-2013 | | выбор заказчика | шт | 10 | | 2 шт. на поворот |
| 20 | Тройник канализационный ПП 45° (врезки ветвей) | ГОСТ 32414-2013 | | выбор заказчика | шт | 4 | | |
| 21 | Ревизия канализационная ПП (после поворота трассы) | ГОСТ 32414-2013 | | выбор заказчика | шт | 5 | | доступ сохранить |
| 22 | Фитинги PP-R Ø20: тройники, угольники 90° (ветви и повороты В1, Т3) | ГОСТ 32415-2013 | | выбор заказчика | шт | 22 | | |
| 23 | Водорозетка PP-R Ø20×½" настенная, с креплением | ГОСТ 32415-2013 | | выбор заказчика | шт | 8 | | коды — лист выводов |
| | Узлы ввода, люки, короба | | | | | | | |
| 24 | Кран шаровой латунный Ду15 PN16 (отключение ввода) | аналог | | выбор заказчика | шт | 2 | | Ст В1-1, Ст Т3-1 |
| 25 | Фильтр сетчатый косой Ду15 | аналог | | выбор заказчика | шт | 2 | | |
| 26 | Счётчик воды крыльчатый Ду15 (ХВ, ГВ), с поверкой | аналог | | выбор заказчика | шт | 2 | | пломба УК |
| 27 | Клапан обратный Ду15 | аналог | | выбор заказчика | шт | 2 | | |
| 28 | Люк ревизионный нажимной под плитку 300×400 мм | аналог | | выбор заказчика | шт | 1 | | к стоякам и арматуре |
| 29 | Звукоизоляция стояка К1 в коробе: рулонный звукоизоляционный материал ≥ 10 мм, обмотка стояка на высоту этажа | аналог | | выбор заказчика | м | 2,7 | | Ст К1-1 |
| 30 | Короб К1 над полом: профиль ПН/ПС, ГКЛВ 12,5 мм под плитку | аналог | | выбор заказчика | м | 0,6 | | сечение — лист разводки |

## Примечания


1. Форма 1 ГОСТ 21.110-2013, ширины граф изменены по п. 4.1. «Аналог» — аналог по характеристикам: модели внести до черновых работ, привязки выводов сверить по паспортам.
2. Бытовая техника не входит (показана арматура подключения), мойка — в комплекте кухни. Длины труб — трасса листа разводки + подъёмы + 10 %.
3. Стояк К1 в коробе — звукоизоляция стояка в коробе без жёсткого контакта короба с трубой.
4. Расчёт систем водоснабжения и канализации, диаметры магистралей и подбор оборудования выполняет проектная организация.

| | | | | | | |
|---|---|---|---|---|---|---|
| | | | | | Проект: Квартира 58 м² | |
| | Лист | № док. | Подпись | Дата | Спецификация сантехнического оборудования | Стадия: П; Лист: 14; Листов: 60 |
| Дизайнер | Кырпан А.С. | | | 09.10.26 | | |

выпуск 09.10.2026 № 6e771c53bc · стр. 14 из 60

## Примечания

1. Размеры проёмов и привязки — в миллиметрах от чистых граней стен до отделки; привязка — от угла того помещения, со стороны которого стоит размер. Размер в ведомости — ширина × высота проёма от чистого пола 0,000. Откос от угла помещения до проёма с коробкой — не менее 50 мм.
2. Марки в кружках — типы заполнения проёмов (ГОСТ 21.501-2018, п. 5.3.2); одна марка — один типоразмер; количество сверено с планом.
3. Открывание: Л — петли слева, П — справа, если смотреть со стороны, куда открывается полотно (на себя).
4. Скрытые двери (Д-2…Д-4): проём замерить в чистоте; блок заказать до штукатурки (≈ 30 дн.), короб ставить до штукатурки; полотно навесить после чистовой отделки, красить в цвет стен. Порядок практика монтажа, изготовитель подтверждает.
5. Д-2…Д-4 — существующие проёмы, до техзаключения не расширять.
6. Экспликация помещений — лист 3; в марках помещений — номер и площадь, м².
7. Привязка проёма к углу помещения меньше 1 мм на листе, размер на плане не показан: Д-3 — 40 мм; Д-4 — 40 мм.

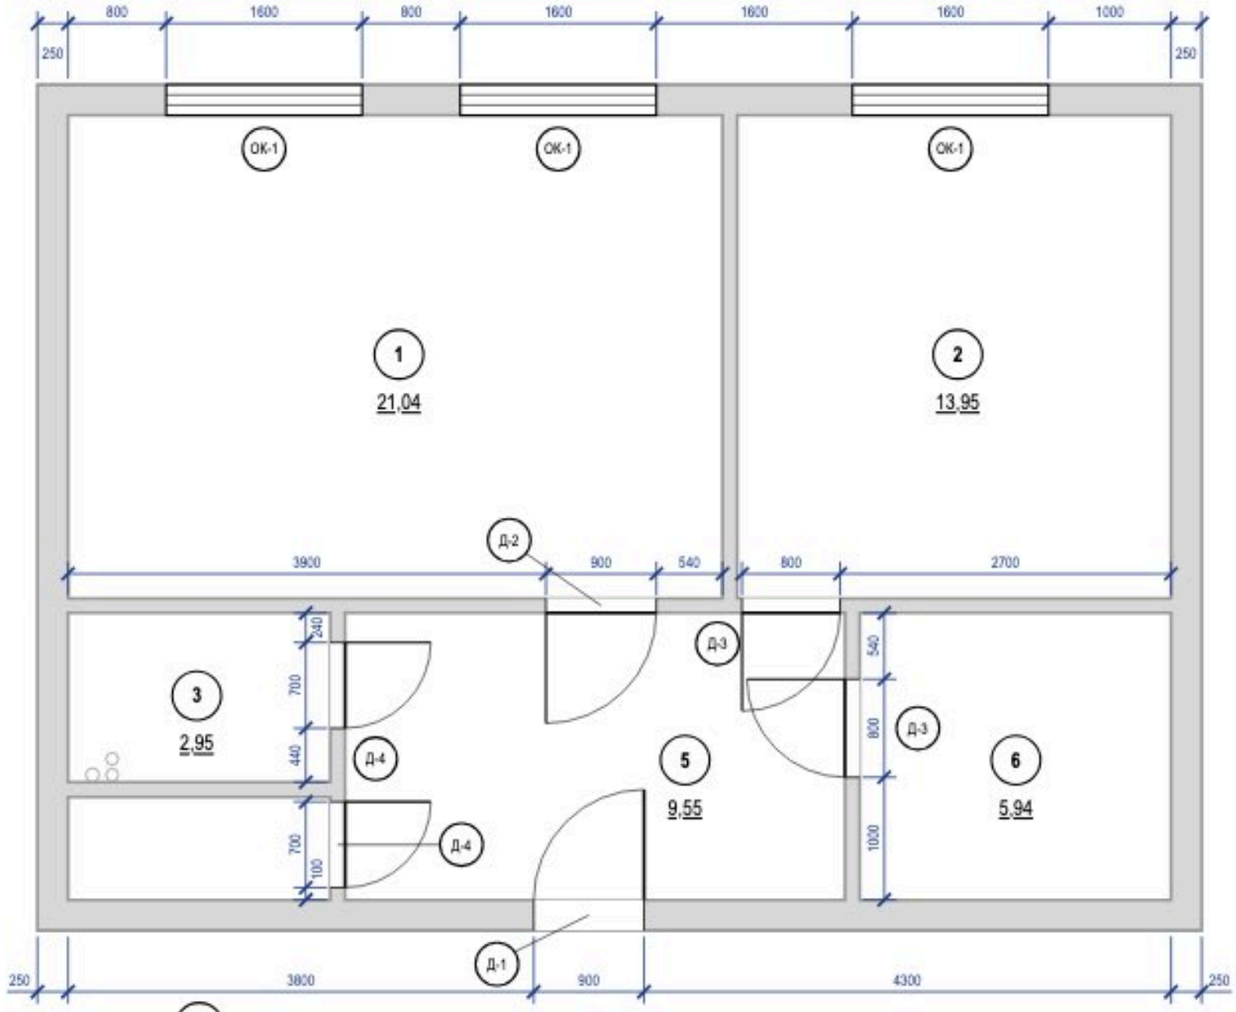



### Ведомость заполнения проёмов

| Марка | Наименование, обозначение | Проём ш×в, мм | Кол. | Откр. | Отделка полотна | Фурнитура | Прим. |
|---|---|---|---|---|---|---|---|
| Д-1 | Блок дверной входной, ГОСТ 31173-2016 | 900×2100 | 1 | Л | в комплекте блока | в комплекте блока (замки, глазок) | |
| Д-2 | Дверь скрытого монтажа, ТУ изготовителя | 900×2100 | 1 | Л | S 1502-Y50R — пом. 5, S 1002-Y50R — пом. 1 | скрытые петли 3D, магнитный замок | |
| Д-3 | Дверь скрытого монтажа, ТУ изготовителя | 800×2100 | 2 | Л, Л | окраска S 1502-Y50R с двух сторон; S 1502-Y50R — пом. 5, V503 — пом. 6 | скрытые петли 3D, магнитный замок | |
| Д-4 | Дверь скрытого монтажа, ТУ изготовителя | 700×2100 | 2 | П, П | S 1502-Y50R — пом. 5, в тон облицовки — пом. 3; S 1502-Y50R — пом. 5, в тон облицовки — пом. 4 | скрытые петли 3D, магнитный замок, фиксатор WC | порог 15 |
| ОК-1 | Блок оконный, ГОСТ 23166-2021 | 1600×1600 | 3 | | | | низ 800 |

| | | | | | Проект: Квартира 58 м² | | | |
|---|---|---|---|---|---|---|---|---|
| | Лист | № док. | Подпись | Дата | План размещения дверей | Стадия | Лист | Листов |
| Дизайнер | Кырпан А.С. | | | 09.10.26 | | П | 15 | 60 |

выпуск 09.10.2026 № 6e771c53bc · стр. 15 из 60

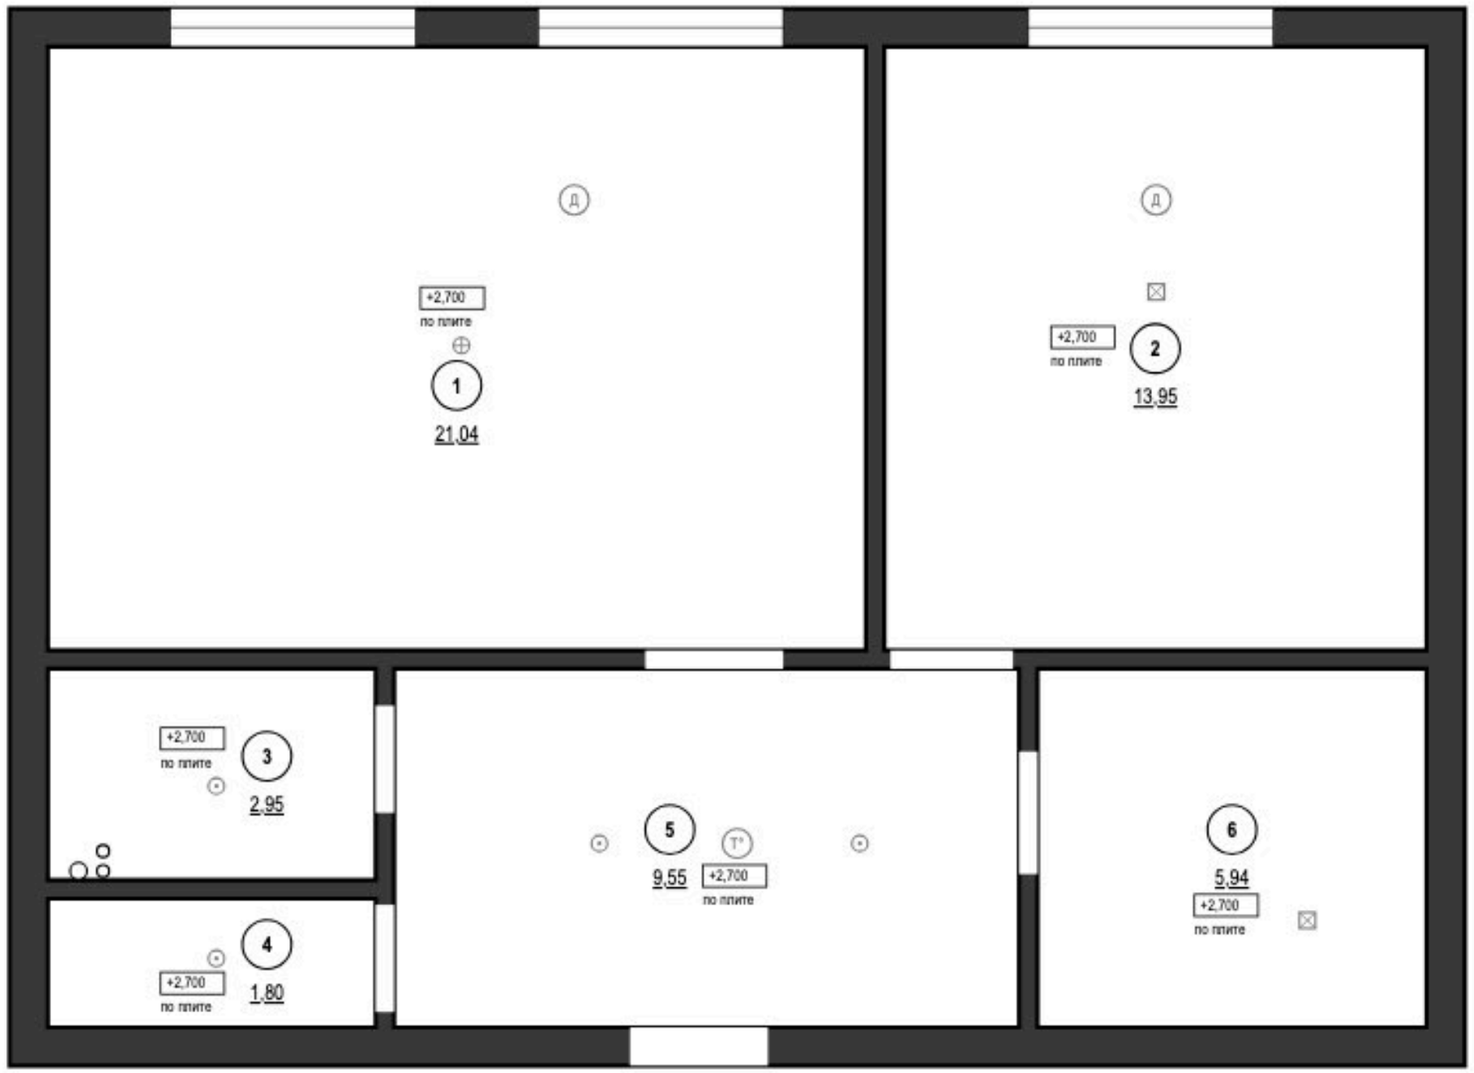


### Ведомость потолков

| Пом. | Марка | Конструкция | Низ | S, м² | Q |
|---|---|---|---|---|---|
| 1 | | по плите, окраска | +2,700 | 21,04 | |
| 2 | | по плите, окраска | +2,700 | 13,95 | |
| 3 | | по плите, окраска | +2,700 | 2,95 | |
| 4 | | по плите, окраска | +2,700 | 1,80 | |
| 5 | | по плите, окраска | +2,700 | 9,55 | |
| 6 | | по плите, окраска | +2,700 | 5,94 | |
| | | **Итого** | | **55,23** | |

### Ведомость вырезов и закладных в потолке

| Марка | Устройство | Кол. | Пом. |
|---|---|---|---|
| | Светильник встраиваемый (марки — план освещения) | 4 | 3, 4, 5 |
| | Светильник накладной (марки — план освещения) | 2 | 2, 6 |
| | Светильник подвесной (марки — план освещения) | 1 | 1 |
| | Извещатель дымовой | 2 | 1, 2 |
| | Извещатель тепловой | 1 | 5 |


### Примечания

1. За отметку ±0,000 принят уровень чистого пола сухих помещений (готовое покрытие), а не существующего пола; пол пом. 3, 4 — −0,015; верх плиты перекрытия −0,064 — расчётный по пирогу пола, не замерен; существующий пол снимается до плиты, его отметка не замерена. Отметки в прямоугольниках — низ потолка; низ плиты перекрытия +2,700. Марка потолка — одна конструкция и отметка на весь альбом.
2. Светильники и потолочные устройства — подложка с планов освещения, слаботочных систем и вентиляции (положение — по ним); вырезы и закладные — по ведомости на листе, до обшивки; отверстия не совмещать с профилями.
3. Пом. 1, 2, 3, 4, 5, 6 — потолок по плите без подвесной системы; отделка — по ведомости отделки.

| | | | | | |
|---|---|---|---|---|---|
| | | | | | Проект: Квартира 58 м² |
| | Лист | № док. | Подпись | Дата | План потолков |
| Дизайнер | Кырпан А.С. | | | 09.10.26 | |

| Стадия | Лист | Листов |
|---|---|---|
| П | 16 | 60 |

выпуск 09.10.2026 № 6e771c53bc · стр. 16 из 60

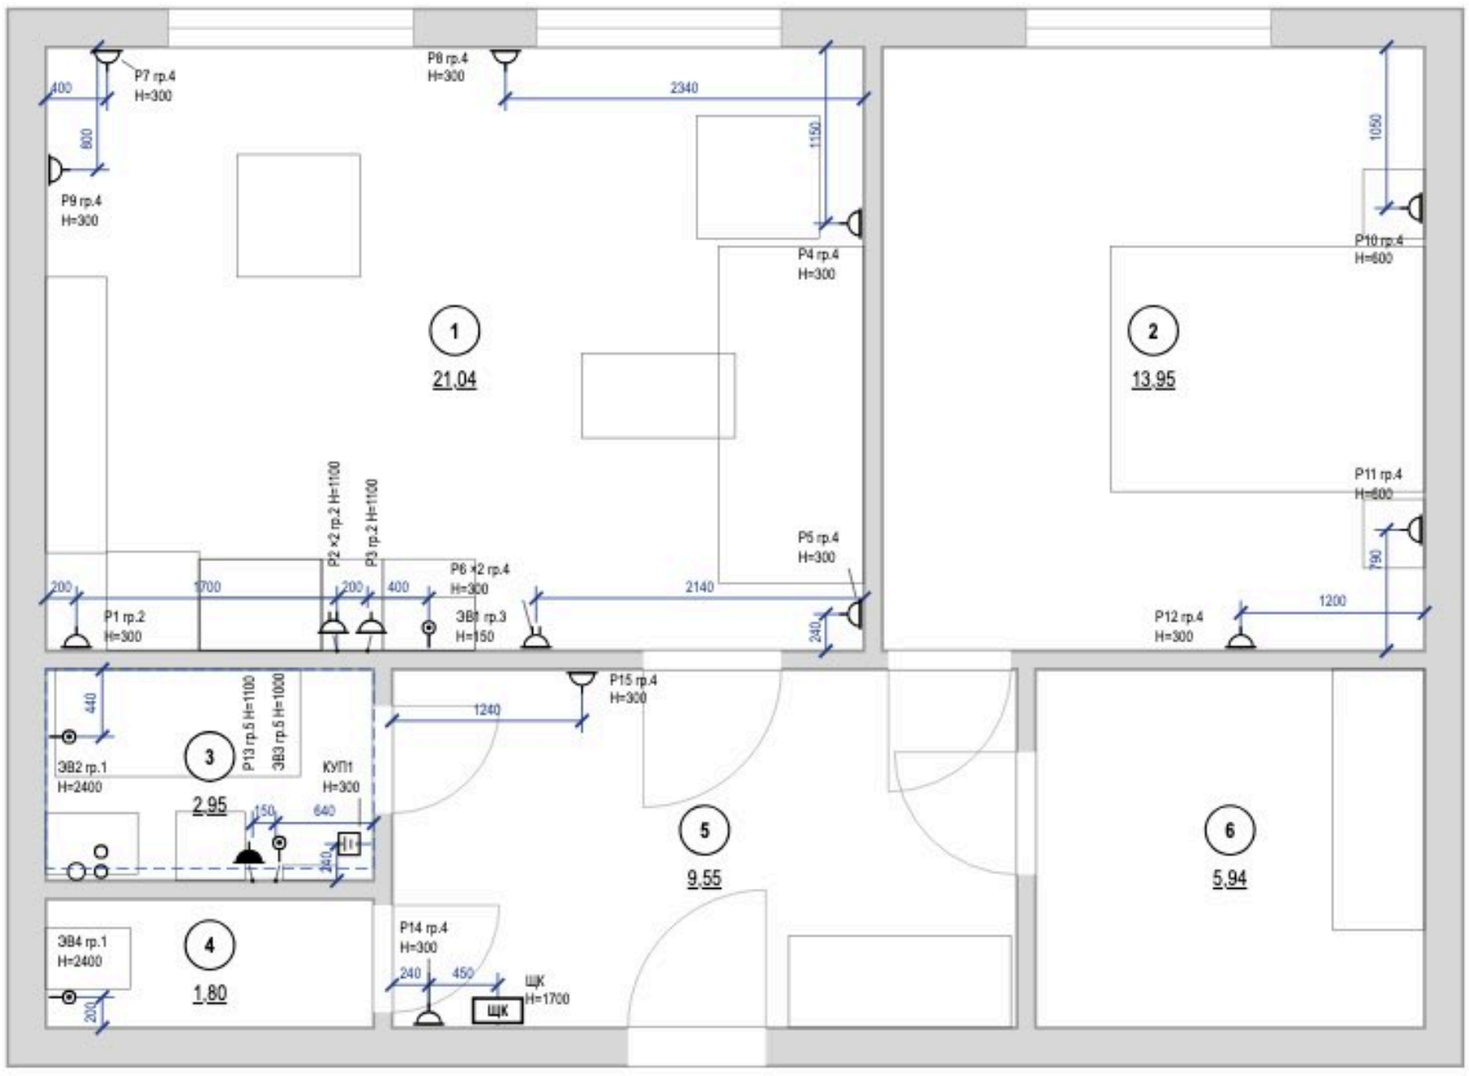


## Условные обозначения


- розетка с заземляющим контактом; у знака — марка, ×N постов в рамке, гр. — группа щита, Н — высота оси, мм
- то же, рамка на 2 поста (число черточек — число постов)
- розетка влагозащищённая IP44
- вывод кабеля для подключения прибора (без розетки), марка ЭВ
- КУП — коробка уравнивания потенциалов (ДСУП), проводник к шине PE щита
- ЩК — щит квартирный
- знак разведён для читаемости: точка на стене — у выноски, привязка — до неё
- граница зоны 2 ванной (600 мм от ванны/поддона)
- мебель и сантехприборы — подложка
- стояк К1 — канализация, В1 — ХВС, Т3 — ГВС
- 1 — номер помещения, площадь м²

## Примечания

1. За отметку 0,000 принят уровень чистого пола. Высоты Н — от чистого пола до оси изделия; привязки — от чистовой грани стены до оси механизма (у рамки на несколько постов — до оси рамки).
2. Высота установки, не указанная на плане: розетки — 300 мм от чистого пола; выводы кабеля — по паспорту прибора.
3. Розетки в санузле — только вне зон 0–2 (ПУЭ 7.1.48, ГОСТ Р 50571.7.701-2024), IP44, через УЗО 30 мА.
4. Розеточные и мокрые линии — через УЗО или дифавтомат с током утечки не более 30 мА (ПУЭ 7.1.79); в санузле выполнить ДСУП (ПУЭ 7.1.87–7.1.88).
5. Кабель — медный, исполнение нг(A)-LS (ГОСТ 31565-2012); скрытая прокладка только горизонтально и вертикально; фактические трассы зафиксировать исполнительной схемой до закрытия отделкой.
6. Расчёт нагрузок, токов КЗ, селективности и сечений — по проекту ЭОМ организации с допуском СРО; лист задаёт состав, расположение и группы.
7. Выводы кухонной техники — после утверждения проекта кухни (ориентировочно); привязки выводов даны от осей модулей гарнитура и пересматриваются вместе с проектом кухни.
8. Ведомости электроточек, изделий, светильников и расшифровка клавиш — лист «Ведомость электроточек и изделий».

| | | | | | | | | |
|---|---|---|---|---|---|---|---|---|
| | | | | | Проект: Квартира 58 м² | | | |
| | Лист | № док. | Подпись | Дата | План розеток и электровыводов | Стадия | Лист | Листов |
| Дизайнер | Кырпан А.С. | | | 09.10.26 | | П | 17 | 60 |

выпуск 09.10.2026 № 6e771c53bc · стр. 17 из 60

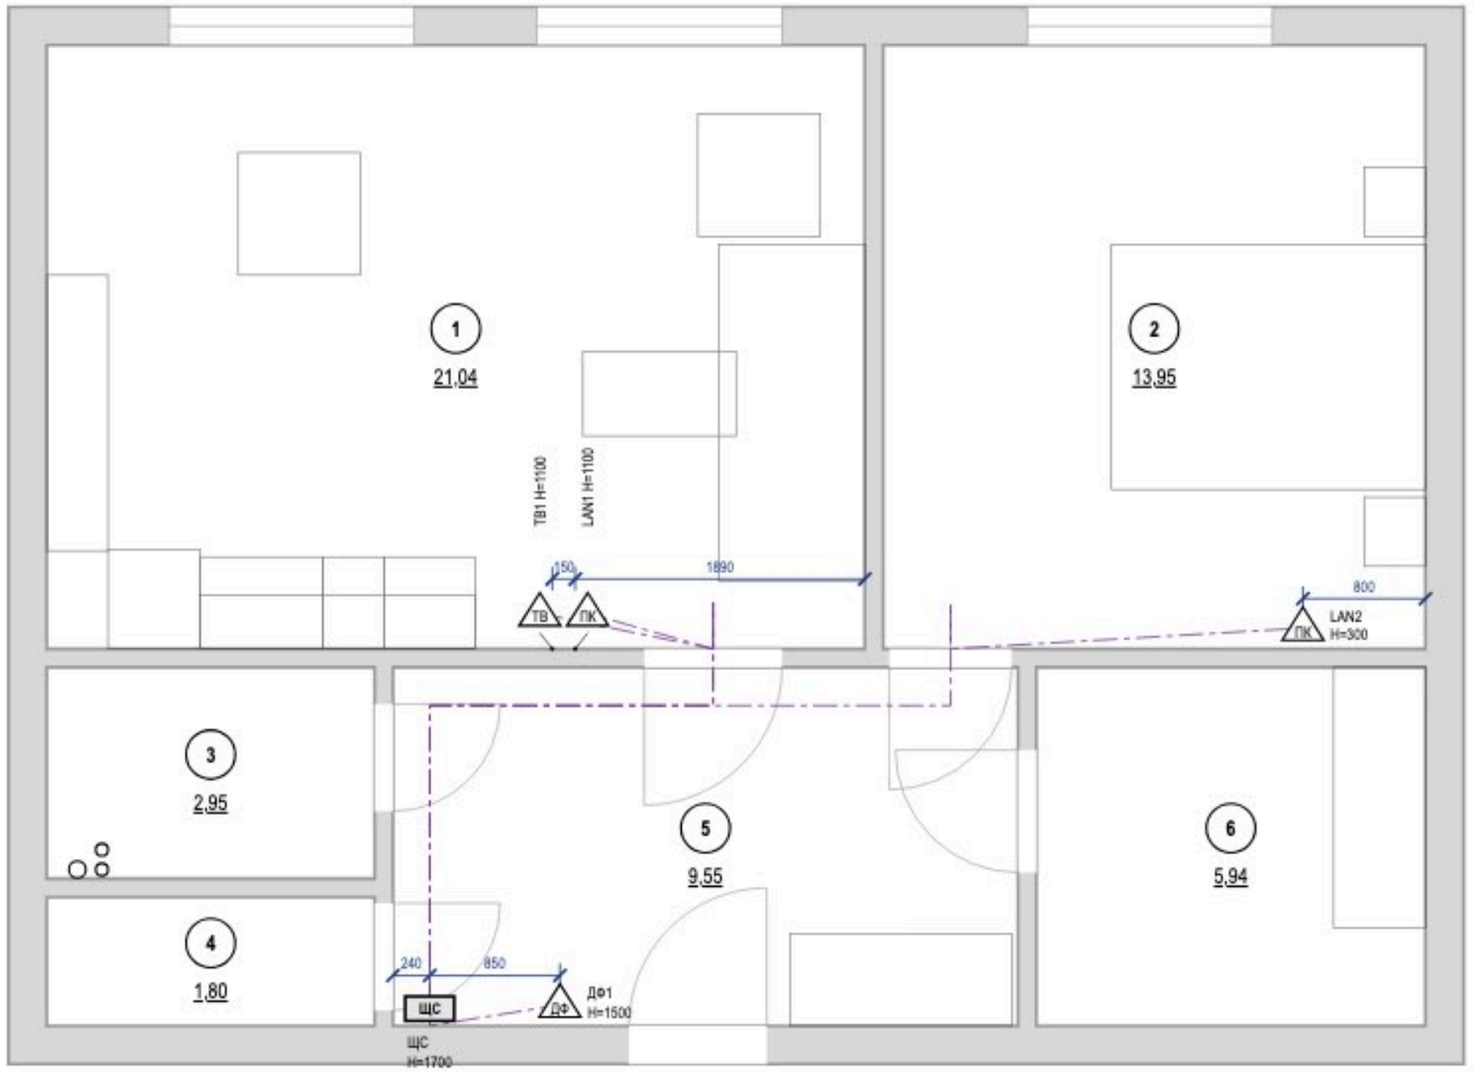



**Примечания**

1. За отметку 0,000 принят уровень чистого пола. Высоты H — от чистого пола до оси изделия; привязки — от чистовой грани стены до оси механизма (у рамки на несколько постов — до оси рамки).
2. Высота установки, не указанная на плане: розетки LAN и ТВ — 300 мм от чистого пола.
3. Слаботочные кабели — отдельно от силовых: в своей трубе или лотке, при параллельной прокладке не ближе 100 мм к силовым, пересечения под прямым углом; каждую точку — отдельным кабелем от ЩС без скруток.
4. Трассы на листе — принципиальные; фактические зафиксировать исполнительной схемой до закрытия отделкой. Силовые линии, УЗО 30 мА, ДСУП, кабель нг(A)-LS — по листам розеток и щита.
5. Проект силовой части и расчёт токов КЗ — по проекту ЭОМ; слаботочная часть согласуется с провайдером и управляющей компанией (домофон, коллективное ТВ).

| | | | | | |
|---|---|---|---|---|---|
| | | | | | Проект: Квартира 58 м² |
| | Лист | № док. | Подпись | Дата | План слаботочных сетей |
| Дизайнер | Кырпан А.С. | | | 09.10.26 | |

| Стадия | Лист | Листов |
|---|---|---|
| П | 18 | 60 |

выпуск 09.10.2026 № 6e771c53bc · стр. 18 из 60

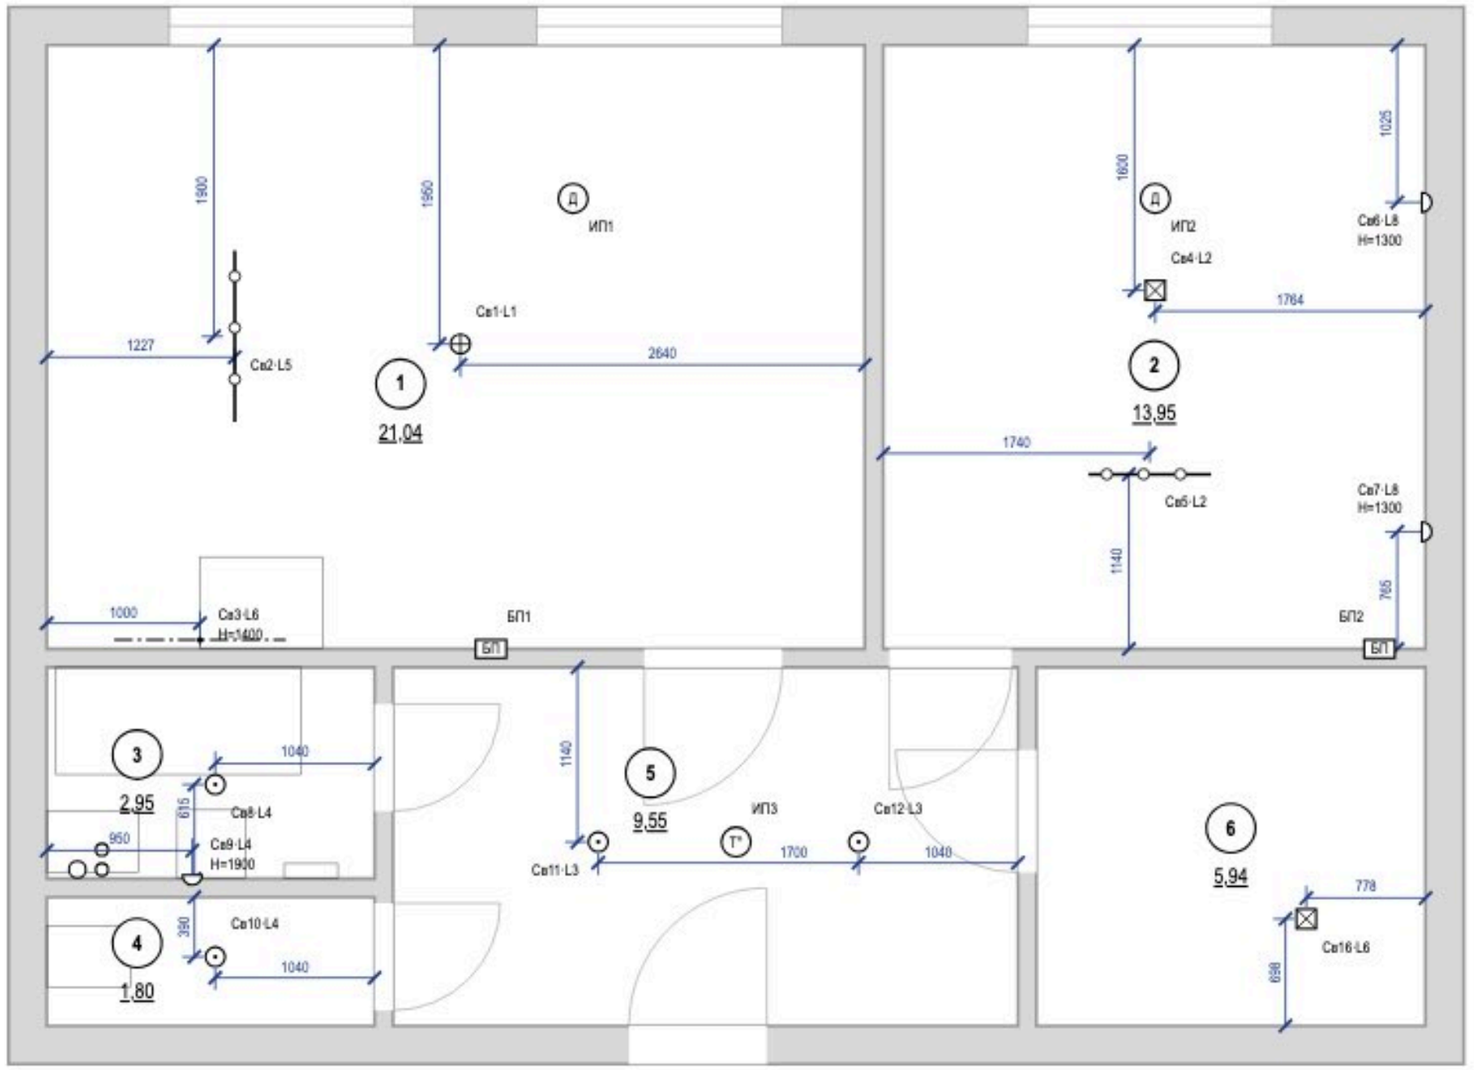


## Примечания

1. За отметку 0,000 принят уровень чистого пола. Высоты H — от чистого пола до оси изделия; привязки — от чистовой грани стены до оси механизма (у рамки на несколько постов — до оси рамки).
2. Высота установки, не указанная на плане: светильники — на потолке; настенные — по отметке H у знака. Привязки — до оси светильника от чистовой грани стены, по рядам.
3. Освещённость: Eн — СанПиН 1.2.3685-21, табл. 5.52 (на полу); Φ треб. = Eн·Sr[U·MF) при U = 0,5 и MF = 0,71 (СП 52.13330.2016, табл. 4.3) — оценка, не светотехнический расчёт. Декоративная подсветка в Φ не входит.
4. Во влажных помещениях — светильники не ниже IP44; в зонах 0–2 ванной — по ГОСТ Р 50571.7.701-2024 (зона 1 — IPX5).
5. Розеточные и мокрые линии — через УЗО или дифавтомат с током утечки не более 30 мА (ПУЭ 7.1.79); в санузле выполнить ДСУП (ПУЭ 7.1.87–7.1.88).
6. Кабель — медный, исполнение нг(A)-LS (ГОСТ 31565-2012); скрытая прокладка только горизонтально и вертикально, фактические трассы зафиксировать исполнительной схемой до закрытия отделкой.
7. Расчёт нагрузок, токов КЗ, селективности и сечений — по проекту ЭОМ организации с допуском СРО; лист задаёт состав, расположение и группы.
8. Ведомость светильников — лист «Ведомость электроточек и изделий».

| | | | | | |
|---|---|---|---|---|---|
| | | | | | Проект: Квартира 58 м² |
| | Лист | № док. | Подпись | Дата | План освещения |
| Дизайнер | Кырпан А.С. | | | 09.10.26 | |

| Стадия | Лист | Листов |
|---|---|---|
| П | 19 | 60 |

выпуск 09.10.2026 № 6e771c53bc · стр. 19 из 60

## Спецификация светильников

| Поз. | Марки | Наименование | Установка | Кол. | P, Вт | Σ P, Вт | Ф, лм | Tц, K | Ra | Угол, ° | IP | Дим. | Группа | Пом. |
|---|---|---|---|---|---|---|---|---|---|---|---|---|---|---|
| 1 | Св1 | Подвесной | подвес | 1 | 40 | 40 | 3600 | 3000 | 90 | — | 20 | — | L1 | 1 |
| 2 | Св2 | Трековая система | на потолке | 4 | 12 | 48 | 950 | 3000 | 90 | — | 20 | — | L5 | 1 |
| 3 | Св3 | Линейный настенный | под верхними шкафами, H=1400 | 1 | 14 | 14 | 1080 | 3000 | 90 | — | 20 | — | L6 | 1 |
| 4 | Св4 | Потолочный накладной | на потолке | 1 | 36 | 36 | 3200 | 2700 | 90 | — | 20 | — | L2 | 2 |
| 5 | Св5 | Трековая система | на потолке | 2 | 12 | 24 | 900 | 2700 | 90 | — | 20 | — | L2 | 2 |
| 6 | Св6, Св7 | Настенный (бра) | на стене, H=1300 | 2 | 4 | 8 | 250 | 2700 | 90 | — | 20 | — | L8 | 2 |
| 7 | Св8 | Встраиваемый точечный | встраиваемый | 1 | 9 | 9 | 700 | 3000 | 90 | — | 44 | — | L4 | 3 |
| 8 | Св9 | Настенный (бра) | над зеркалом, H=1900 | 1 | 6 | 6 | 400 | 3000 | 90 | — | 44 | — | L4 | 3 |
| 9 | Св10 | Встраиваемый точечный | встраиваемый | 1 | 6 | 6 | 500 | 3000 | 90 | — | 44 | — | L4 | 4 |
| 10 | Св11, Св12 | Встраиваемый точечный | встраиваемый | 2 | 9 | 18 | 800 | 3000 | 90 | — | 20 | — | L3 | 5 |
| 11 | Св16 | Потолочный накладной | на потолке, засветка стены | 1 | 10 | 10 | 900 | 3000 | 90 | — | 20 | — | L6 | 6 |
| | | **Итого** | | **17 шт** | | **219** | | | | | | | | |

## Слои света по помещениям

| Пом. | Помещение | Слои света и группы включения (марки светильников) | Tц, K | Ra | Σ P, Вт | Сцен. |
|---|---|---|---|---|---|---|
| 1 | Кухня-гостиная | общий — L1 (Св1), L5 (Св2); рабочий — L6 (Св3) | 3000 | 90 | 102 | — |
| 2 | Спальня | общий — L2 (Св4, Св5); рабочий — L8 (Св6, Св7) | 2700 | 90 | 68 | — |
| 3 | Ванная | общий — L4 (Св8); рабочий — L4 (Св9) | 3000 | 90 | 15 | — |
| 4 | Санузел | общий — L4 (Св10) | 3000 | 90 | 6 | — |
| 5 | Прихожая | общий — L3 (Св11, Св12) | 3000 | 90 | 18 | — |
| 6 | Гардеробная | общий — L6 (Св16) | 3000 | 90 | 10 | — |

## LED-ленты, линейные светильники и блоки питания

| Марка | Пом. | L, м | U, В | Вт/м | Σ P, Вт | БП | P БП, Вт | Загр., % | Питание | Доступ к БП |
|---|---|---|---|---|---|---|---|---|---|---|
| Св2 | 1 | 1,2 | 24 | — | 48 | БП1 | 100 | 62 | встроенный ввод | H=2300 |
| — | 1 | 1,8 | 24 | — | 14 | БП1 | 100 | 62 | встроенный ввод | H=2300 |
| Св5 | 2 | 0,8 | 24 | — | 24 | БП2 | 60 | 40 | встроенный ввод | H=2300 |

## Сценарии освещения

Сценарии не заданы: группы включаются клавишами по плану выключателей (лист 21).

## Слои света

общий — равномерный свет помещения, по норме освещённости

рабочий — местный свет задачи: столешница, зеркало, чтение у кровати


## Примечания

1. Позиции и марки Св — те же, что на плане освещения (лист 19) и в ведомости светильников (лист «Ведомость электроточек и изделий»); группы L — по плану выключателей (лист 21).
2. Модели светильников не назначены: подбор по графам спецификации — поток, Tц, Ra, угол, IP и диммирование не хуже указанных, мощность не больше. IP 20 — сухие помещения.
3. Мощность и поток — по паспортам принятых изделий, Σ P — установленная мощность освещения. Оценка освещённости — на плане освещения; это не светотехнический расчёт.

| | | | | | |
|---|---|---|---|---|---|
| | | | | | Проект: Квартира 58 м² |
| | Лист | № док. | Подпись | Дата | Спецификация светильников и сценарии освещения |
| Дизайнер | Кырпан А.С. | | | 09.10.26 | |

| Стадия | Лист | Листов |
|---|---|---|
| П | 20 | 60 |

выпуск 09.10.2026 № 6e771c53bc · стр. 20 из 60

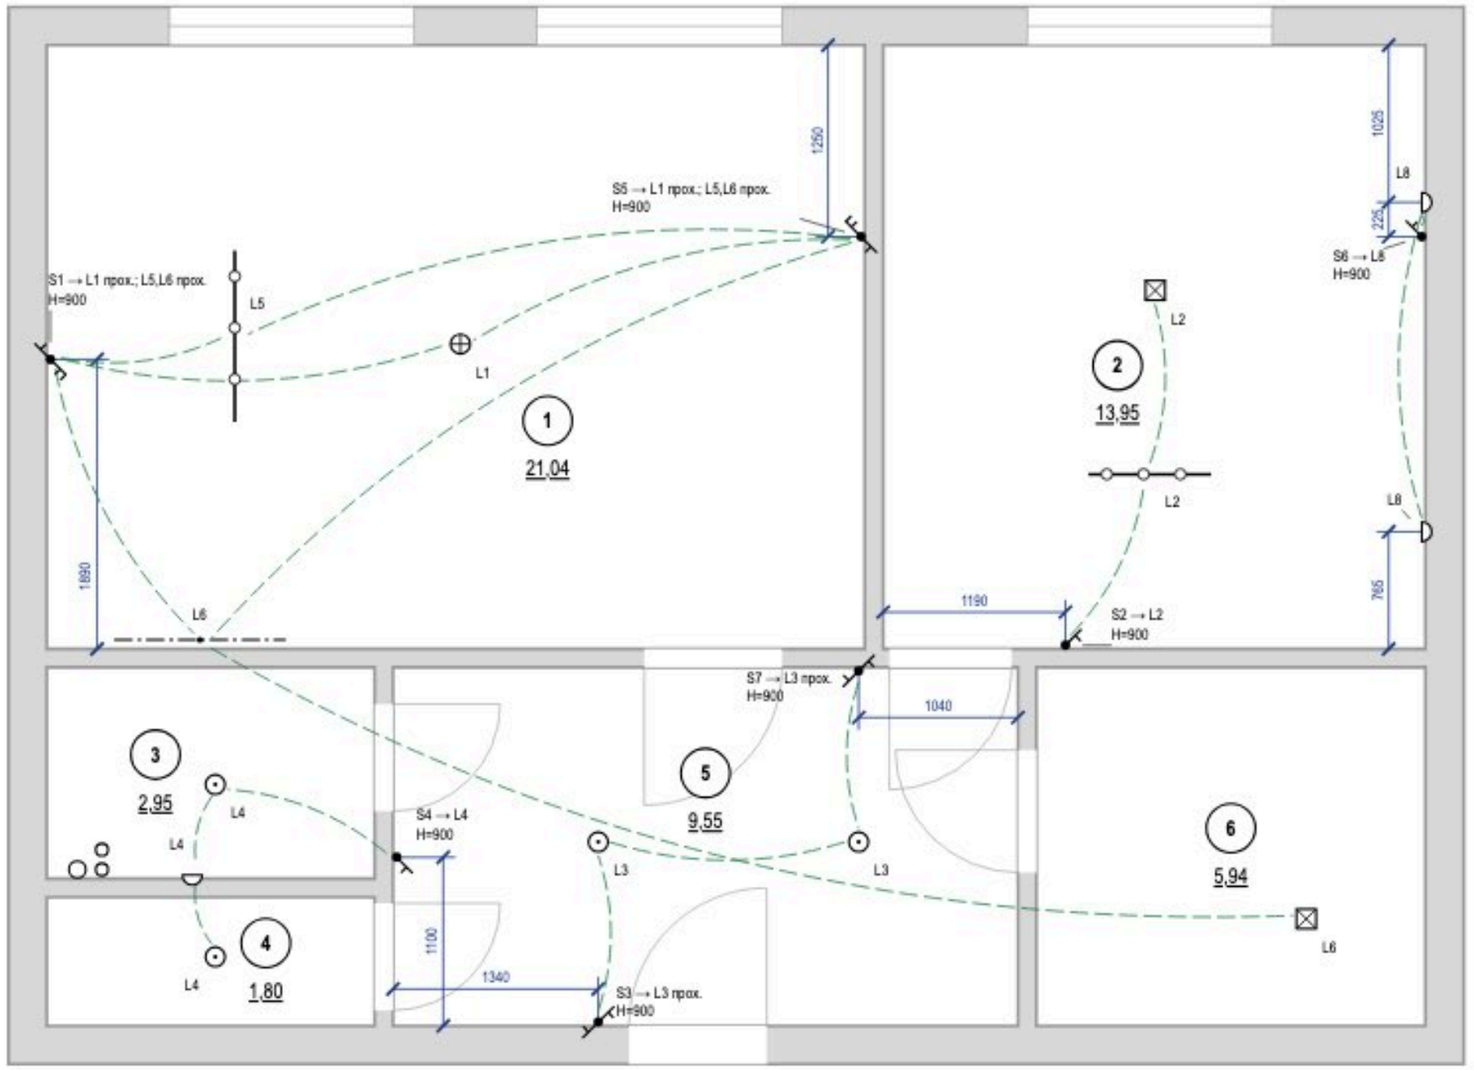


**Примечания**

1. За отметку 0,000 принят уровень чистого пола. Высоты H — от чистого пола до оси изделия; привязки — от чистовой грани стены до оси механизма (у рамки на несколько постов — до оси рамки).
2. Высота установки, не указанная на плане: выключатели — 900 мм от чистого пола, со стороны дверной ручки (ПУЭ 7.1.51).
3. Линии связи показывают, какой выключатель какую группу L включает; это не трасса кабеля. Трасса — принципиальная, фактическую зафиксировать исполнительной схемой.
4. Группы из нескольких мест (L1 — S1, S5; L5 — S1, S5; L6 — S1, S5; L3 — S3, S7): на крайних местах — проходные клавиши, на промежуточных — перекрёстные; механизмы — в ведомости изделий.
5. Вентиляторы санузлов (выводы ЭВ на плане розеток) включаются вместе с основным светом помещения, отключаются с задержкой — таймер выбега в вентиляторе.
6. Розеточные и мокрые линии — через УЗО или дифавтомат с током утечки не более 30 мА (ПУЭ 7.1.79); в санузле выполнить ДСУП (ПУЭ 7.1.87–7.1.88).
7. Кабель — медный, исполнение нг(A)-LS (ГОСТ 31565-2012); скрытая прокладка только горизонтально и вертикально, фактические трассы зафиксировать исполнительной схемой до закрытия отделкой.
8. Расчёт нагрузок, токов КЗ, селективности и сечений — по проекту ЭОМ организации с допуском СРО; лист задаёт состав, расположение и группы.
9. Расшифровка клавиш и ведомость изделий — лист «Ведомость электроточек и изделий».

| | | | | | |
|---|---|---|---|---|---|
| | | | | | Проект: Квартира 58 м² |
| | Лист | № док. | Подпись | Дата | Управление светильниками |
| Дизайнер | Кырпан А.С. | | | 09.10.26 | |

| Стадия | Лист | Листов |
|---|---|---|
| П | 21 | 60 |

выпуск 09.10.2026 № 6e771c53bc · стр. 21 из 60




## Условные обозначения

- стояк: К1 — канализация, В1 — ХВС, Т3 — ГВС
- номер помещения, площадь м²
- вытяжная решётка в вентканал: марка, расход м³/ч, Н центра от чистого пола
- вытяжная решётка с бытовым вентилятором и обратным клапаном: марка, расход, Н
- бризер (приток с фильтром и подогревом)
- переток: зазор под полотном или переточная решётка
- кухонная вытяжка над варочной панелью
- воздуховод кухонной вытяжки в коробе под потолком
- отдельный вход воздуховода в вентканал, обратный клапан
- внутренний блок кондиционера (КВ-N)
- наружный блок (КН-N) на фасаде / в корзине
- трасса фреонопровода и межблочного кабеля
- дренаж конденсата (уклон стрелкой)
- отверстие в наружной стене под трассу

## Воздухообмен, м³/ч

| № | Помещение | Выт. норма | Выт. проект | Прит. норма | Прит. проект | Устройства |
|---|---|---|---|---|---|---|
| 1 | Кухня-гостиная | 60 | 60 | 60 | 60 | ВР1, Б1 |
| 2 | Спальня | | | 60 | 60 | Б2 |
| 3 | Ванная | 50 | 60 | | | ВР2 |
| 4 | Санузел | 25 | 60 | | | ВР2 |
| 6 | Гардеробная | 3 | | | | переток |
| | **Итого** | **138** | **180** | **60** | **120** | |

Воздухообмен квартиры — по большей из сумм притока и вытяжки: норма 138 м³/ч, проект 180 м³/ч.
Вытяжка не меньше притока — баланс сведён.

## Кондиционеры

| Марка | Помещение | Нар. блок | Трасса, м | Дренаж |
|---|---|---|---|---|
| КВ-1 | 1. Кухня-гостиная | КН-1 | 3,0 п | наружу, i=50 мм/м |
| КВ-2 | 2. Спальня | КН-2 | 3,0 п | наружу, i=50 мм/м |


## Примечания

1. Расчёт систем ОВ и подбор оборудования — проектная организация с допуском СРО; лист даёт места, трассы и привязки.
2. Нормы вытяжки — СП 54.13330.2022 (Изм. 1, 2), табл. 7.1: кухня с электроплитой 60 м³/ч, с газовой 100; ванная и совмещённый санузел 50; уборная 25; гардеробная 0,2 ч⁻¹. Приток в жилые — 3 м³/ч на 1 м² (менее 20 м² общей площади на человека), иначе 30 м³/ч на человека.
3. Вентканалы и шахты не сужать, не переносить и не закрывать; вентилятор и кухонная вытяжка — через обратный клапан, без перекрытия естественной тяги.
4. Кухонная вытяжка в воздухообмен не включена: воздуховод не менее Ø125 в коробе, вход в канал отдельный.
5. Переток — зазор под полотнами межкомнатных дверей или переточная решётка.
6. Дренаж кондиционера — непрерывный уклон 40–60 мм/м без контруклонов (СТО НОСТРОЙ 2.23.1-2011, п. 5.8.4); врезка в К1 — через сифон (п. 5.8.9); длина трассы и перепад высот — по паспорту блока; внутренний блок — не ближе 150 мм к потолку, не над кроватью и рабочим местом.
7. Наружный блок на фасаде многоквартирного дома — с согласия собственников (общее имущество); при наличии корзин — только в них.
8. «п» в графе «Трасса» — трасса фреона по плану короче минимума, разница выбрана компенсационной петлёй (бухтой): КВ-1 — по плану 0,8 м, с петлёй 3,0 м; КВ-2 — по плану 0,8 м, с петлёй 3,0 м. Длина петли принята по минимуму трассы (3,0 м) и зависит от паспорта модели кондиционера, которая ещё не выбрана: минимум и максимум трассы — типовые, по паспорту модели, до заказа сверить и при необходимости изменить петлю или место наружного блока. Бухту уложить в коробе или за внутренним блоком, не в штробе.
9. Привязки оборудования — по паспортам приобретённых моделей, до черновых работ.

| | | | | | |
|---|---|---|---|---|---|
| | | | | | Проект: Квартира 58 м² |
| | Лист | № док. | Подпись | Дата | |
| Дизайнер | Кырпан А.С. | | | 09.10.26 | План вентиляции |

| Стадия | Лист | Листов |
|---|---|---|
| П | 22 | 60 |

выпуск 09.10.2026 · 6e771c53bc · стр. 22 из 60

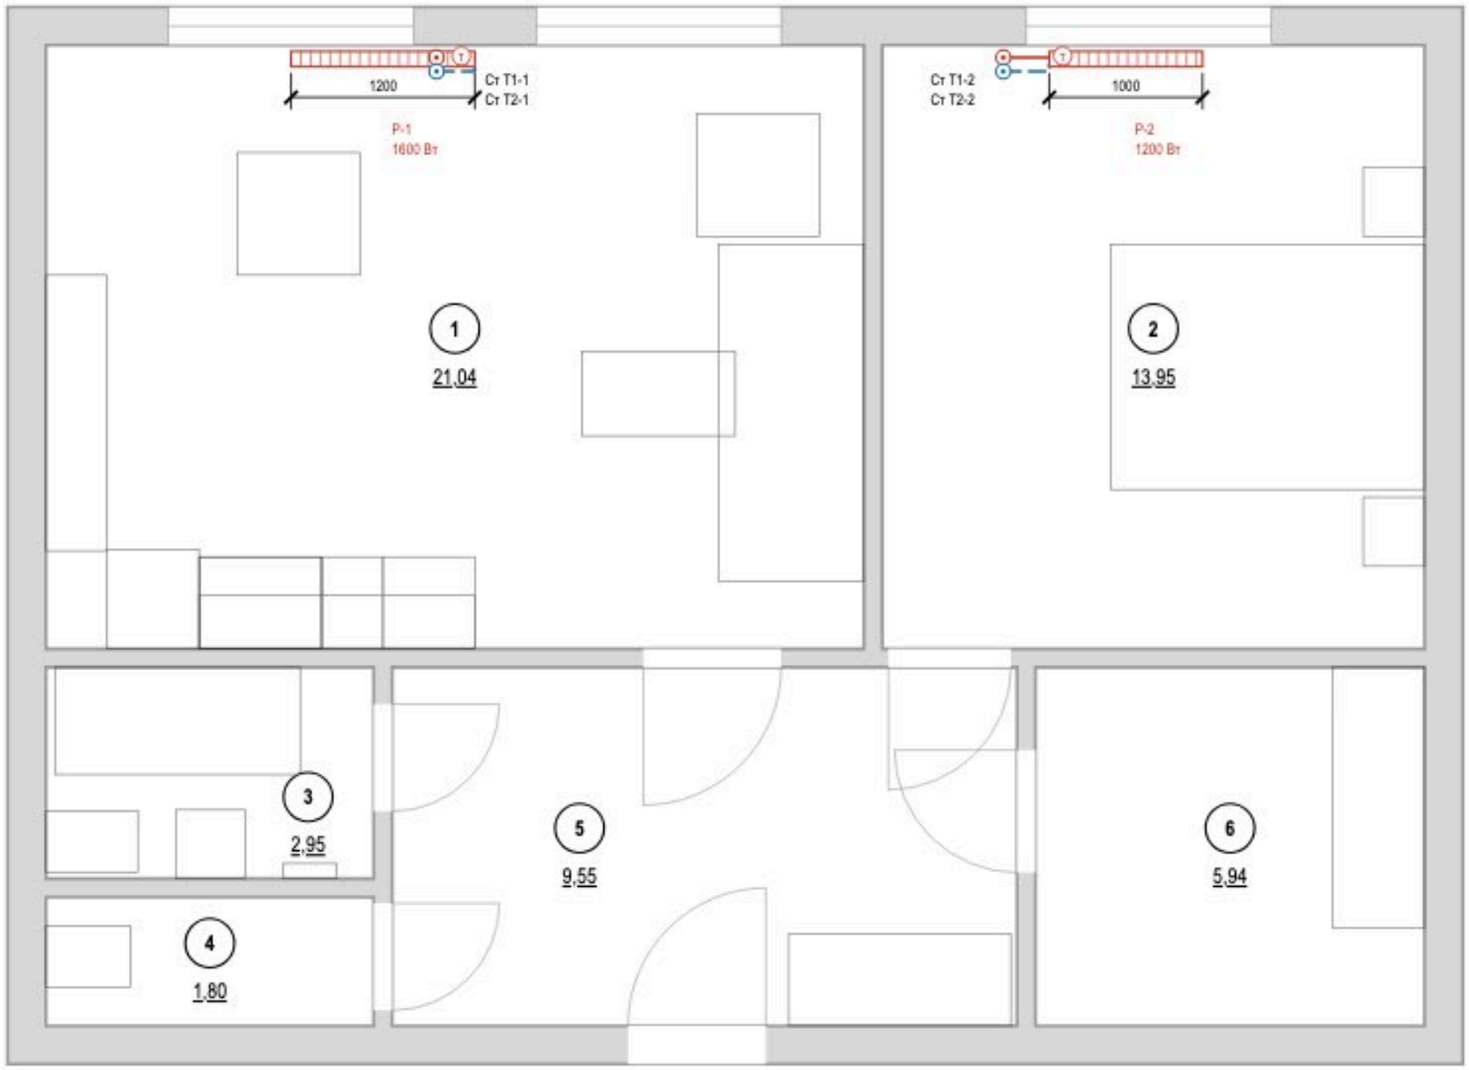


## Условные обозначения

- (1) — номер помещения, площадь м²
- радиатор отопления (марка РО-N, длина по плану)
- (Т) — клапан с термоголовкой на подаче
- стояк отопления, подающий (Ст Т1-N)
- стояк отопления, обратный (Ст Т2-N)
- Т1 — отопление, подающий трубопровод
- Т2 — отопление, обратный трубопровод

## Ведомость радиаторов

| Марка | Помещение | Тип | Д×В×Г, мм | Низ / стена | Q, Вт |
|---|---|---|---|---|---|
| Р-1 | 1. Кухня-гостиная | панельный 22 | 1200×500×100 | 120 / 40 | 1600 |
| Р-2 | 2. Спальня | панельный 22 | 1000×500×100 | 120 / 40 | 1200 |

Низ — от чистого пола, стена — зазор до задней панели, мм.

**Привязки — до обмера**
Стояки отопления в исходных данных не заданы: показаны у откосов окон, подводки — принципиально. До черновых работ — обмер стояков и паспорта приборов; лист перевыпустить по факту.


## Примечания

1. Расчёт системы отопления, теплопотерь и подбор приборов — проектная организация с допуском СРО; лист даёт места и привязки.
2. Тип, длина и мощность радиаторов — по теплотехническому расчёту; лист задаёт места, зазоры и подключение.
3. Зазоры радиатора: низ не менее 100 мм от чистого пола, верх не менее 100 мм до подоконника, 30–50 мм от стены до задней панели; центр по оси окна с допуском ±20 мм.
4. Радиаторы не закрывать глухими коробами и мебелью; перенос и замена приборов в многоквартирном доме — переустройство, согласование с управляющей организацией (ЖК РФ ст. 25–26); вынос на лоджию запрещён.
5. Трубы отопления через межквартирные стены не прокладывать (СП 51.13330.2011, п. 9.19); через перекрытия и перегородки — в гильзах.
6. Привязки приборов и подводок — по паспортам приобретённых радиаторов и клапанов, до черновых работ.
7. До закрытия отделкой трубопроводы отопления испытать гидростатическим давлением с оформлением акта (СП 73.13330.2016, 7.2–7.3).

| | | | | | |
|---|---|---|---|---|---|
| | | | | | Проект: Квартира 58 м² |
| | Лист | № док. | Подпись | Дата | |
| Дизайнер | Кырпан А.С. | | | 09.10.26 | План отопления |

| Стадия | Лист | Листов |
|---|---|---|
| П | 23 | 60 |

выпуск 09.10.2026 № 6e771c53bc · стр. 23 из 60

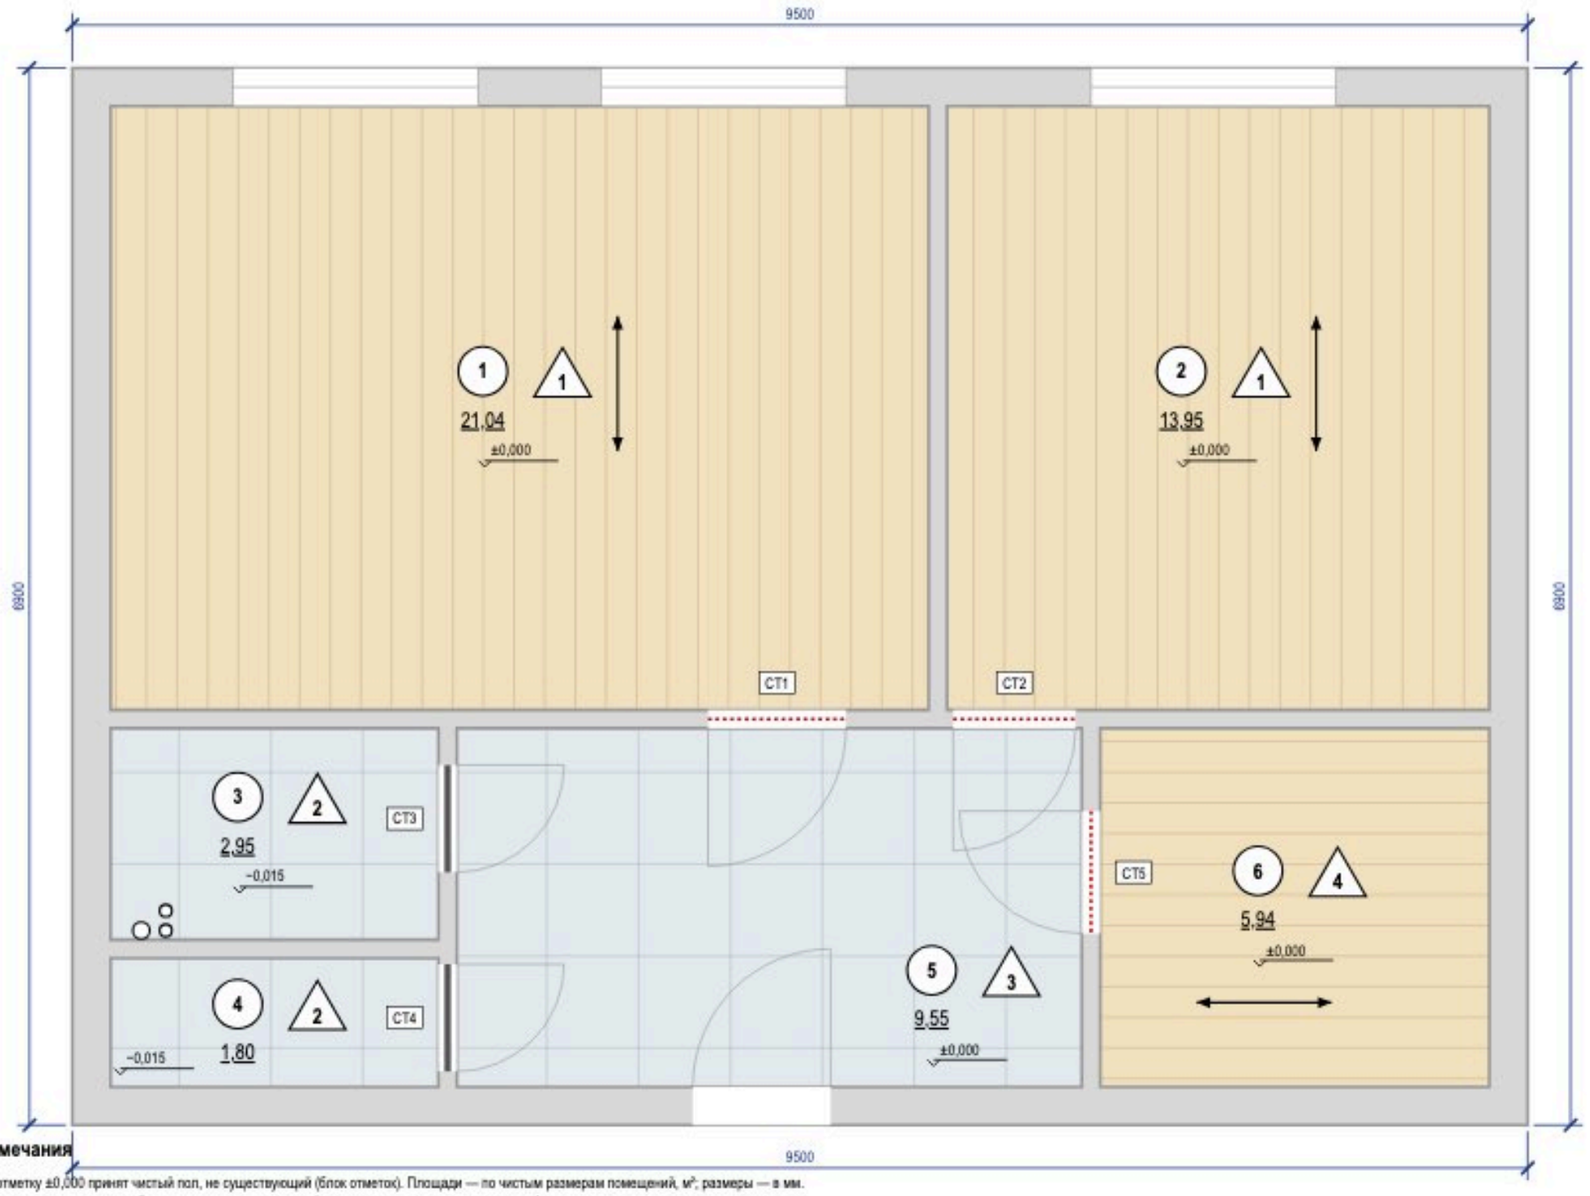


## Экспликация полов

| Номер помещения | Тип пола | Схема пола | Данные элементов пола (наименование, толщина, основание), мм | Площадь, м² |
|---|---|---|---|---|
| 1, 2 | 1 | | Инженерная доска, IM1861, 1380×190 мм, на клею<br>ЧП ±0,000 | 34,99 |
| 3, 4 | 2 | | Керамогранит, SG651622R, 600×600 мм<br>Гидроизоляция обмазочная, 2 слоя, с заведением на стены 200 мм<br>ЧП −0,015 | 4,75 |
| 5 | 3 | | Керамогранит, SG651622R, 600×600 мм<br>ЧП ±0,000 | 9,55 |
| 6 | 4 | | Инженерная доска на клею — 14<br>Стяжка ЦПС М200 — 50<br>Плита перекрытия<br>Всего 64 мм; ЧП ±0,000, верх плиты −0,064 | 5,94 |
| | | | **Итого** | **55,23** |

## Спецификация плинтусов

| Наименование | Помещения | Длина, м (с запасом) |
|---|---|---|
| SX184, h = 110 мм, крепление к стене, окраска в цвет NCS S 0300-N | 1, 2, 5, 6 | 54 |

## Отметки по высоте

**±0,000** — чистый пол пом. 1, 2, 5, 6; отсчёт высот
**−0,015** — чистый пол пом. 3, 4, ниже на 15 мм
**−0,064** — верх плиты — расчёт, не замер (задание на обмер)
**сущ. пол** — снимается до плиты; не замерен (задание на обмер)

## Примечания

1. За отметку ±0,000 принят чистый пол, не существующий (блок отметок). Площади — по чистым размерам помещений, м²; размеры — в мм.
2. Стык разнотипных покрытий — по оси дверного полотна (под полотном в закрытом положении); решение стыка — по ведомости стыков.
3. Пол санузлов ниже смежных помещений на 15 мм за счёт меньшей толщины стяжки (верх плиты общий — по экспликации полов); гидроизоляция по стяжке с заведением на стены не менее 200 мм (СП 29.13330.2011, п. 7.2), до облицовки — тест проливом и акт скрытых работ.
4. Выпуски канализации с уклоном и трассы водоснабжения — в слое засыпки под стяжкой (по экспликации полов); отметки, уклоны и прочистки — по листу разводки ВК 13.
5. Звукоизоляционный слой под стяжкой проектом не предусмотрен (стяжка по плите): приведённый уровень ударного шума перекрытия с полом $L_{nw}$ не более 60 дБ (СП 51.13330.2011, табл. 2) подтвердить по данным дома; при превышении — плавающая стяжка по звукоизоляции с демпферной лентой по контуру и у стояков, пирог пересчитать.
6. Штучные покрытия (инженерная доска): направление — по стрелке; влажность основания по СМ не более 2,0 % (по ТУ изготовителя).
7. Ровность основания — просвет под 2-метровой рейкой не более 2 мм: пом. 1, 2, 6 (инженерная доска), пом. 3, 4, 5 (керамогранит); проверить до укладки покрытия (СП 71.13330.2017, табл. 8.5).
8. Сетка на плитке — условная, в размер формата; точка старта и раскладка — по листу раскладки плитки.
9. Пироги полов — по экспликации полов: слои сверху вниз, толщины в мм; гидроизоляция мокрых зон — в пироге и в ведомости отделки; схема пола — без масштаба.

| | | | | | |
|---|---|---|---|---|---|
| | | | | | Проект: Квартира 58 м² |
| | Лист | № док. | Подпись | Дата | |
| Дизайнер | Кырпан А.С. | | | 09.10.26 | План покрытий пола |

| Стадия | Лист | Листов |
|---|---|---|
| П | 24 | 60 |

выпуск 09.10.2026 № 6e771c53bc · стр. 24 из 60

## Ведомость плитки

| Помещение, поверхность | Плитка, код | Формат | Шов | S, м² | Целых | Подр. | С запасом |
|---|---|---|---|---|---|---|---|
| Ванная, пол | SG651622R | 600×600 | 2 | 2,95 | 2 | 10 | 14 |
| Санузел, пол | SG651622R | 600×600 | 2 | 1,80 | 0 | 8 | 9 |
| Прихожая, пол | SG651622R | 600×600 | 2 | 9,55 | 10 | 18 | 31 |
| **Итого 600×600** | | | | **14,30** | **12** | **36** | **54** |

## Ведомость материалов

| Материал | Класс, код | Норма расхода | Кол-во |
|---|---|---|---|
| Затирка | класс не задан | (a+b)/ab·шов·1,6 | 1,5 кг |
| Клей | C2 S1 | 1,5 кг/м²·мм, слой 5 | 37 кг (2 меш.) |
| Клей | C2 | 1,5 кг/м²·мм, слой 5 | 78 кг (4 меш.) |
| Демпф. лента | по периметру пола из плитки | | 21,2 м |

## Условные обозначения

- плитка целая; тонкая линия — шов
- плитка с подрезкой (размер — на цепочке)
- ось старта; стрелки — направление укладки
- сантехприбор: габарит, высота по практике
- отметка чистого пола на полке выноски, м
- (А) обозначение стены А–Г (как на развёртках)


## Примечания

1. Плитка пола мокрых помещений не задана — планы полов санузлов не выполнены; на листе — ведомость плитки остальных помещений.
2. Толщины облицовки стен не заданы: раскладка от черновых размеров, до укладки пересчитать от чистовых.
3. Раскладка пола «Ванная» и пола «Санузел» и пола «Прихожая» — на листе «Раскладка плитки. Ванная. Санузел. Прихожая».
4. Калибр партии не задан — до укладки замерить (рабочий размер W, ГОСТ 13996-2019) и пересчитать подрезки.
5. Количество: целые по раскладке + по одной на подрезку, запас 10 %; один артикул — одна партия и тон. Исключены поддон, короб, проёмы и места за коробом; S — по чистым граням, как в ведомости отделки.
6. Клей C2 S1; C2 (ГОСТ Р 56387-2018), затирка класс не задан; расход — по ТУ выбранной марки.


| | | | | | | | |
|---|---|---|---|---|---|---|---|
| | | | | | Проект: Квартира 58 м² | | |
| | Лист | № док. | Подпись | Дата | Раскладка плитки. Планы полов | Стадия | Лист | Листов |
| Дизайнер | Кырпан А.С. | | | 09.10.26 | | П | 25 | 60 |

выпуск 09.10.2026 № 6e771c53bc · стр. 25 из 60

Фрагмент 1. Ванная (пом. 3). Пол 600×600, шов 2 мм, М 1:25

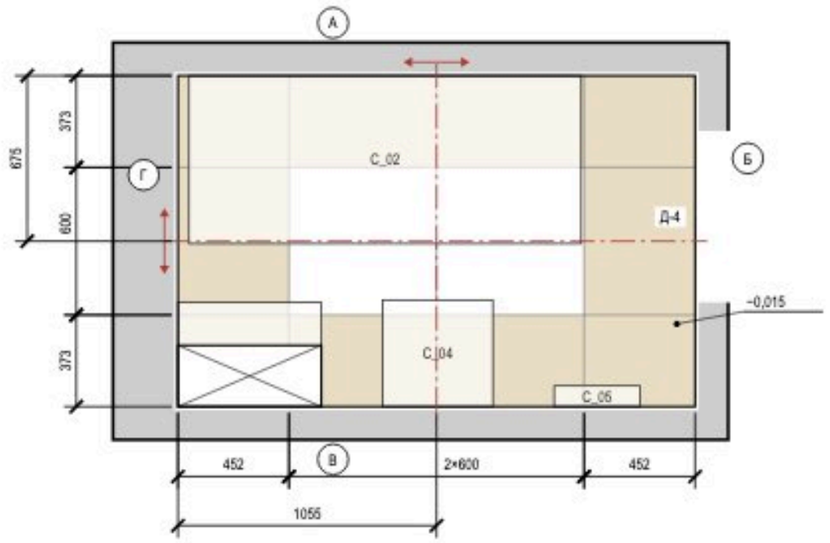


Фрагмент 2. Санузел (пом. 4). Пол 600×600, шов 2 мм, М 1:25

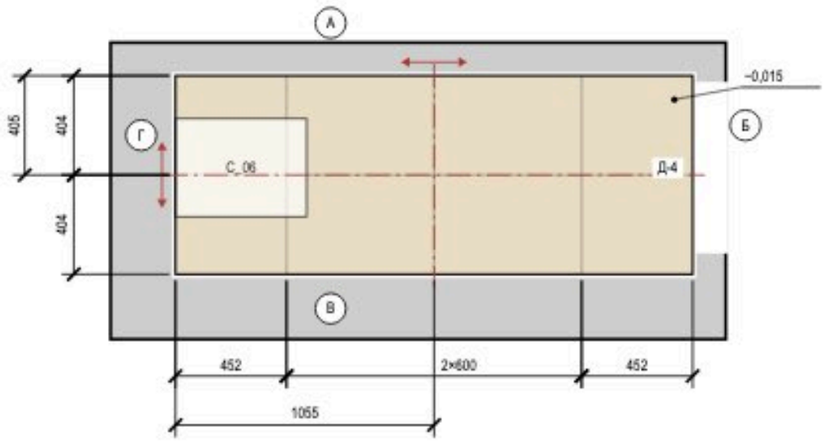


## Условные обозначения

- плитка целая; тонкая линия — шов
- плитка с подрезкой (размер — на цепочке)
- ось старта; стрелки — направление укладки
- отметка чистого пола на полке выноски, м
- А — обозначение стены А–Г (как на развёртках)


## Подсчёт плитки

| Поверхность | Формат | S, м² | Целых | Подр. | С запасом |
|---|---|---|---|---|---|
| Ванная, пол | 600×600 | 2,95 | 2 | 10 | 14 |
| Санузел, пол | 600×600 | 1,80 | 0 | 8 | 9 |
| Прихожая, пол | 600×600 | 9,55 | 10 | 18 | 31 |

## Примечания

1. Ванная: керамогранит 600×600, длинная сторона — вдоль стен Б и Г, шов 2 мм, прямая раскладка от центра. Стены окрашены: раскладка от чистового контура минус штукатурка и шпаклёвка 15 мм на сторону (принято); подрезки 452 / 373 мм, срез — под плинтус.
2. Ванная: деформационный зазор по периметру 8–10 мм под плинтусом; в проёмах — стык с соседним покрытием по оси полотна двери. Клей С2 S1, затирка класс не задан.
3. Санузел: керамогранит 600×600, длинная сторона — вдоль стен Б и Г, шов 2 мм, прямая раскладка от центра. Стены окрашены: раскладка от чистового контура минус штукатурка и шпаклёвка 15 мм на сторону (принято); подрезки 452 / 404 мм, срез — под плинтус.
4. Санузел: деформационный зазор по периметру 8–10 мм под плинтусом; в проёмах — стык с соседним покрытием по оси полотна двери. Клей С2 S1, затирка класс не задан.
5. Прихожая: керамогранит 600×600, длинная сторона — вдоль стен Б и Г, шов 2 мм, прямая раскладка от центра. Стены окрашены: раскладка от чистового контура минус штукатурка и шпаклёвка 15 мм на сторону (принято); подрезки 519 / 552 мм, срез — под плинтус.
6. Прихожая: деформационный зазор по периметру 8–10 мм под плинтусом; в проёмах — стык с соседним покрытием по оси полотна двери. Клей С2, затирка класс не задан.
7. Клей, затирка и итог по форматам — в ведомостях листа «Раскладка плитки. Планы полов».

Фрагмент 3. Прихожая (пом. 5). Пол 600×600, шов 2 мм, М 1:25

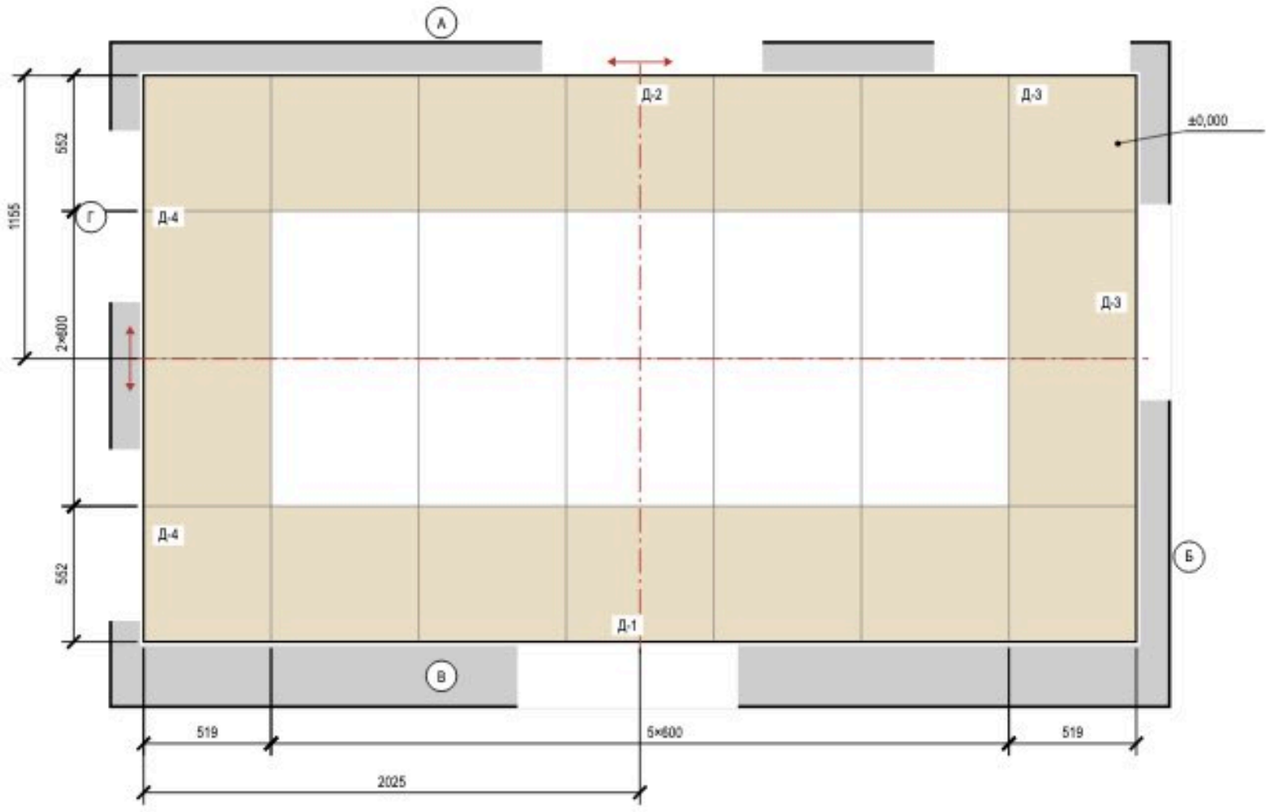


| | | | | | |
|---|---|---|---|---|---|
| | Лист | № док. | Подпись | Дата | Проект: Квартира 58 м² |
| Дизайнер | Кырпан А.С. | | | 09.10.26 | Раскладка плитки. Ванная. Санузел. Прихожая |

| Стадия | Лист | Листов |
|---|---|---|
| П | 26 | 60 |

выпуск 09.10.2026 № 6e771c53bc · стр. 26 из 60



| | | | | | Проект: Квартира 58 м² | | | |
|---|---|---|---|---|---|---|---|---|
| | Лист | № док. | Подпись | Дата | Визуализация кухни-гостиной | Стадия | Лист | Листов |
| Дизайнер | Кырпан А.С. | | | 09.10.26 | | П | 27 | 60 |

выпуск 09.10.2026 № 6e771c53bc · стр. 27 из 60



| | | | | | |
|---|---|---|---|---|---|
| | | | | | Проект: Квартира 58 м² |
| | Лист | № док. | Подпись | Дата | Визуализация кухни-гостиной |
| Дизайнер | Кырпан А.С. | | | 09.10.26 | |

| Стадия | Лист | Листов |
|---|---|---|
| П | 28 | 60 |


выпуск 09.10.2026 № 6e771c53bc · стр. 28 из 60




| | | | | | | |
|---|---|---|---|---|---|---|
| | | | | | Проект: Квартира 58 м² | |
| | Лист | № док. | Подпись | Дата | | |
| Дизайнер | Кырпан А.С. | | | 09.10.26 | Визуализация кухни-гостиной | Стадия / Лист / Листов |
| | | | | | | П / 29 / 60 |

выпуск 09.10.2026 № 6e771c53bc · стр. 29 из 60

## Развёртка стены В

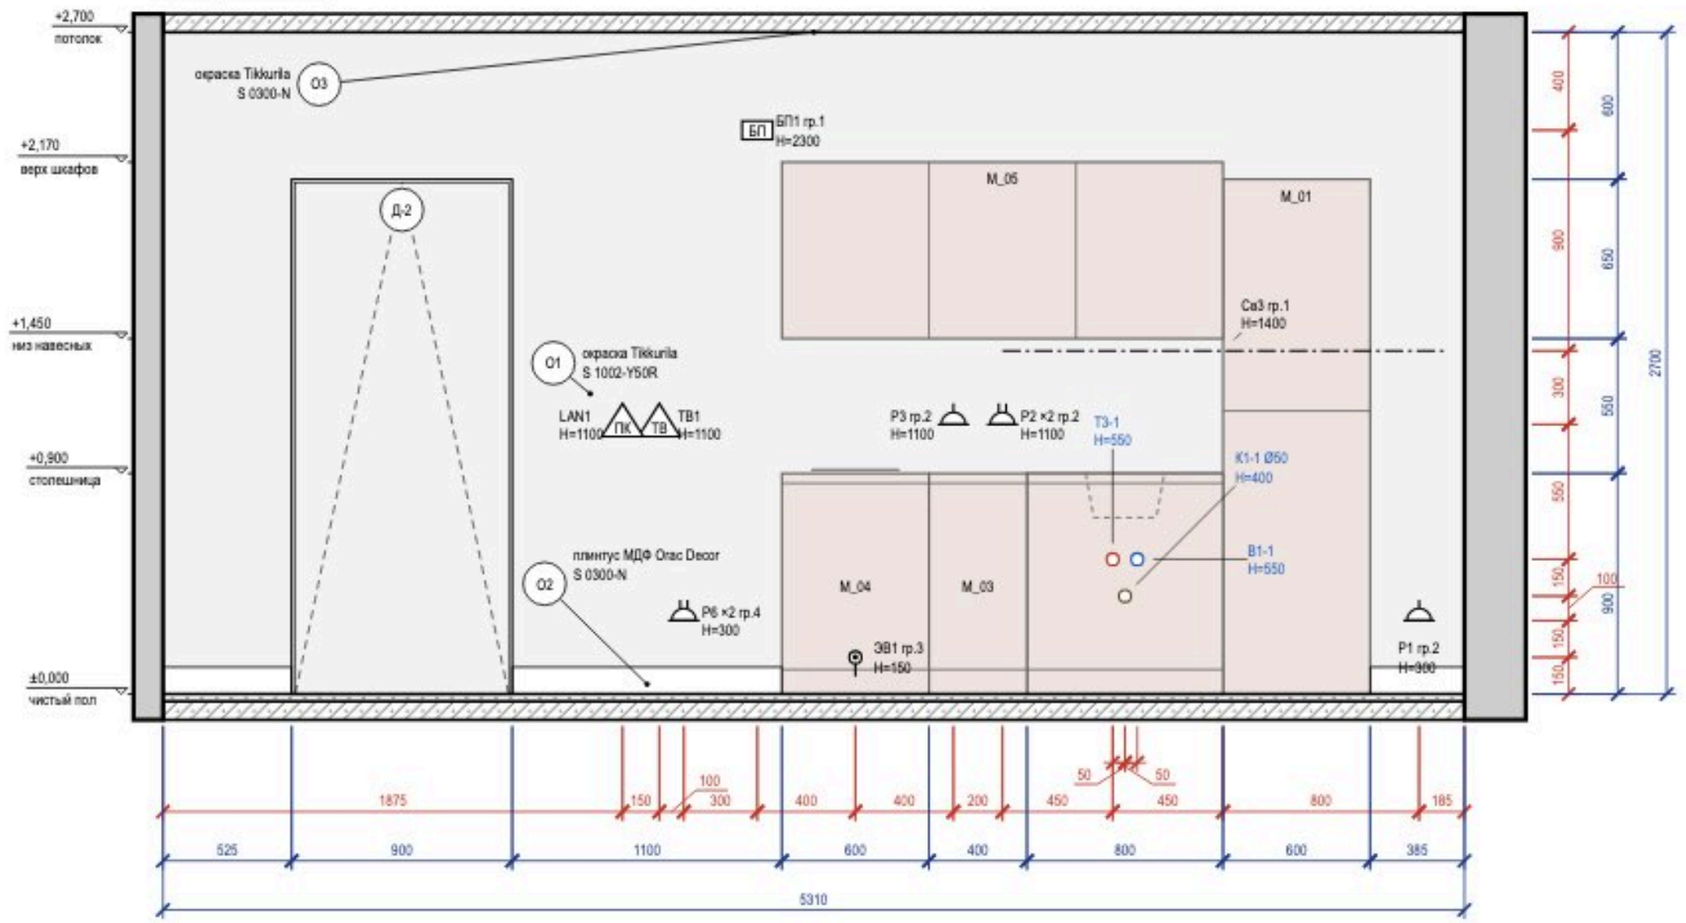



### Схема развёрток (М 1:100)

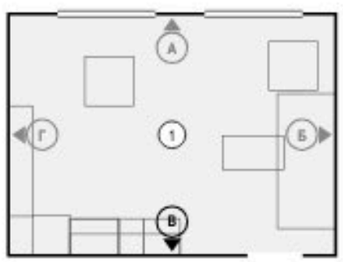


### Ведомость отделки (на листе)

| Марка | Поверхность | Материал, изделие | Цвет, код | Кол. |
|---|---|---|---|---|
| О1 | стены | окраска, Tikkurila, шелковисто-матовая, подготовка Q3 | NCS S 1002-Y50R | 12,4 м² |
| О2 | плинтус | плинтус МДФ, Orac Decor Luxxus, h 110 мм, SX184, шелковисто-матовая | NCS S 0300-N | 2 м |
| О3 | потолок | окраска, Tikkurila, глубокоматовая | NCS S 0300-N | 21 м² |

Визуализация этой стены — лист 28

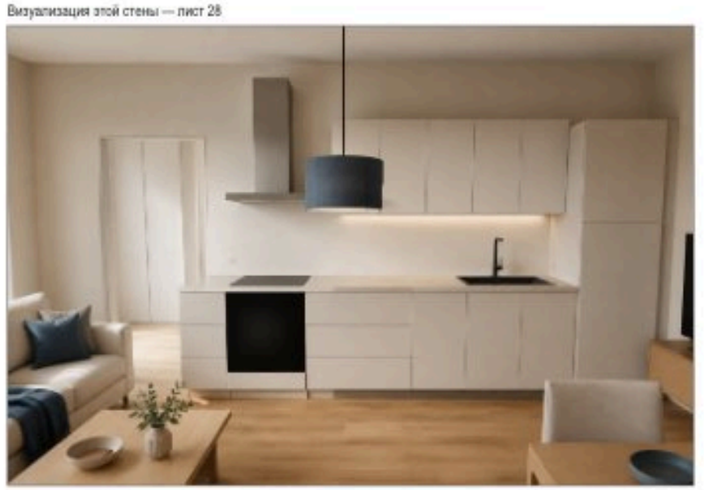

### Примечания


1. Размеры — в мм от чистовых поверхностей стен; условные обозначения и общие указания — лист 2.
2. Двери скрытого монтажа — полотно в плоскости стены, отделка стены по полотну, плинтус прерывается у короба (узел — на листе узлов).
3. Выводы кухонной техники — по утверждённому проекту кухни: привязки выводов даются от осей модулей гарнитура.

| | | | | | |
|---|---|---|---|---|---|
| | | | | | Проект: Квартира 58 м² |
| | Лист | № док. | Подпись | Дата | Развёртка стены В. Кухня-гостиная (пом. 1), кухонный фронт |
| Дизайнер | Кырпан А.С. | | | 09.10.26 | |


| Стадия | Лист | Листов |
|---|---|---|
| П | 30 | 60 |

выпуск 09.10.2026 · 6e771c53bc · стр. 30 из 60

## Развёртка стены А

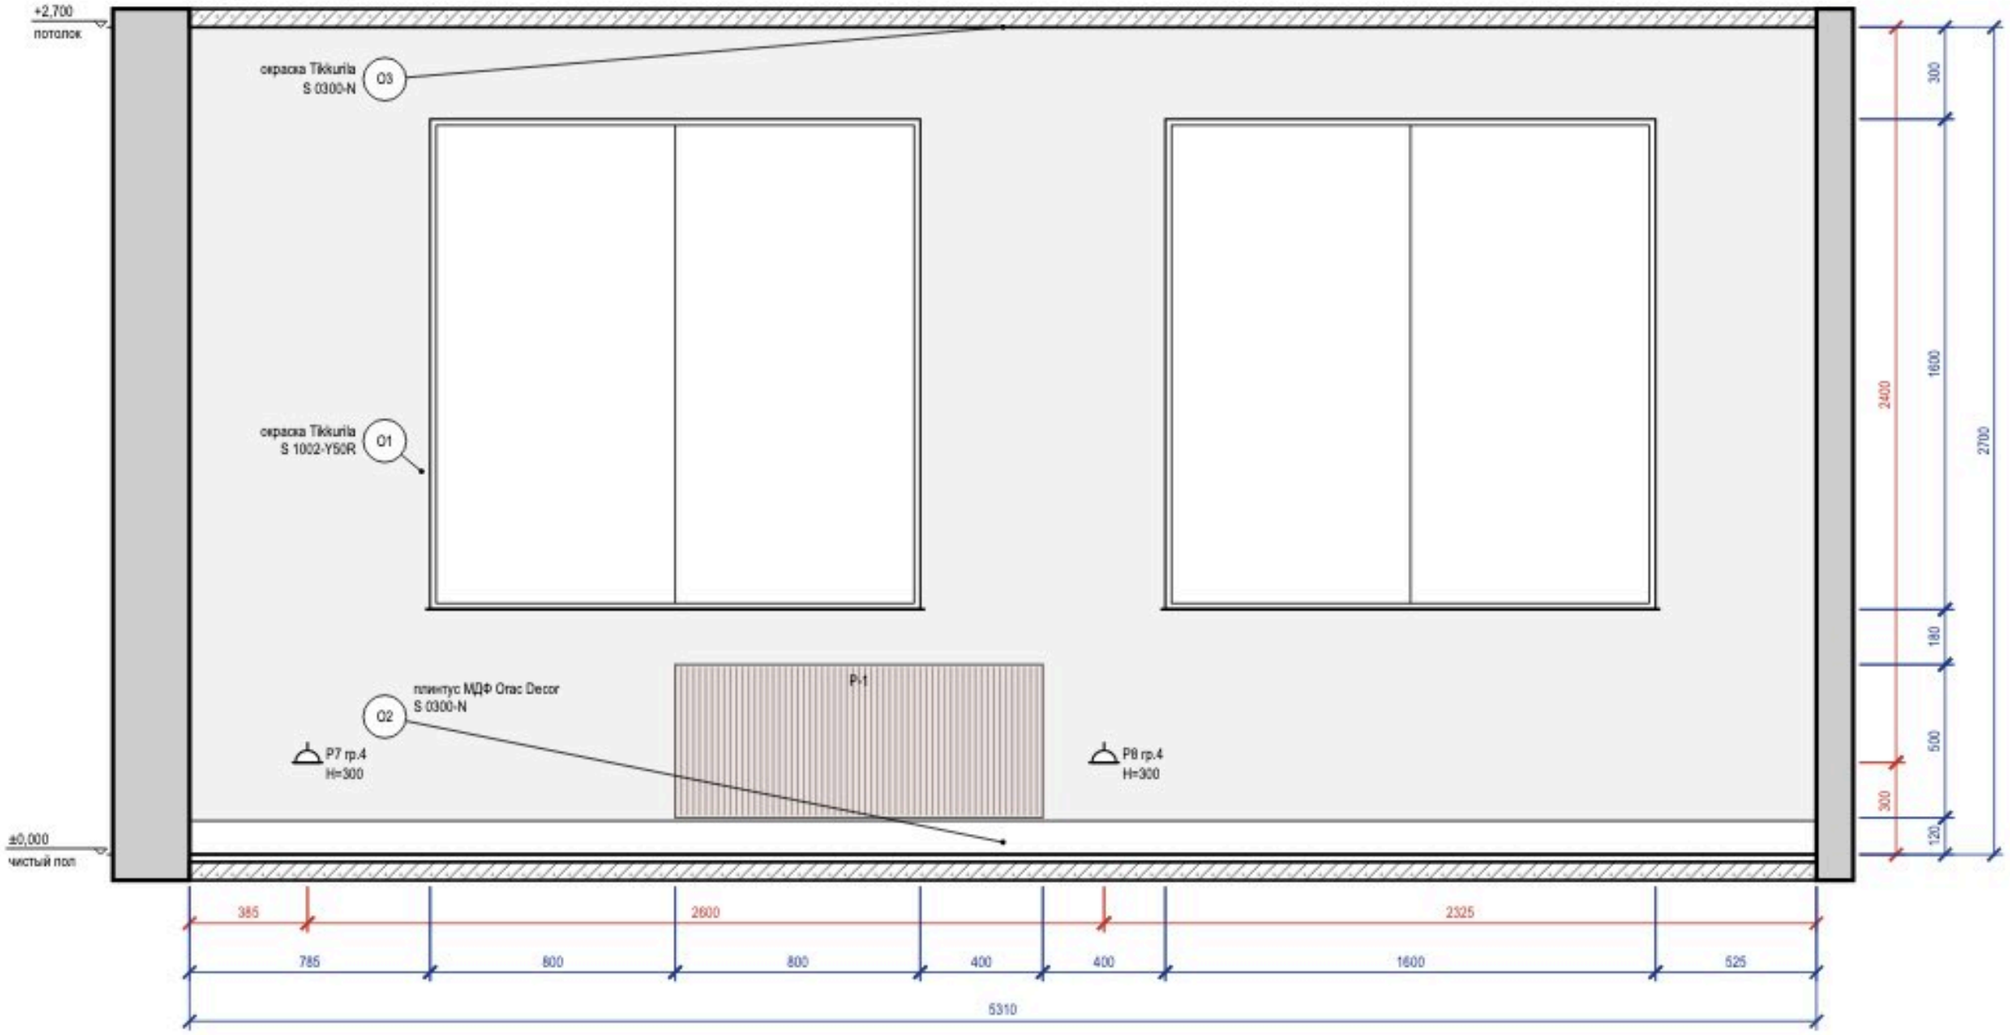


### Схема развёрток (М 1:100)

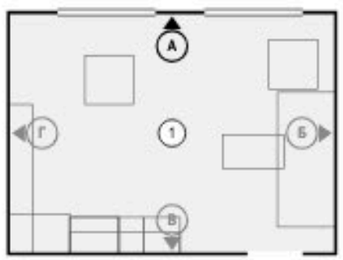


### Ведомость отделки (на листе)

| Марка | Поверхность | Материал, изделие | Цвет, код | Кол. |
|---|---|---|---|---|
| О1 | стены | окраска, Tikkurila, шелковисто-матовая, подготовка О3 | NCS S 1002-Y50R | 9,2 м² |
| О2 | плинтус | плинтус МДФ, Orac Decor Luxxus, h 110 мм, SX184, шелковисто-матовая | NCS S 0300-N | 5,3 м |
| О3 | потолок | окраска, Tikkurila, глубокоматовая | NCS S 0300-N | 21 м² |

### Примечания


1. Размеры — в мм от чистовых поверхностей стен; условные обозначения и общие указания — лист 2.

| | | | | | |
|---|---|---|---|---|---|
| | Лист | № док. | Подпись | Дата | Проект: Квартира 58 м² |
| Дизайнер | Кырпан А.С. | | | 09.10.26 | Развёртка стены А. Кухня-гостиная (пом. 1) |


| Стадия | Лист | Листов |
|---|---|---|
| П | 31 | 60 |

выпуск 09.10.2026 № 6e771c53bc · стр. 31 из 60

## Развёртка стены Б

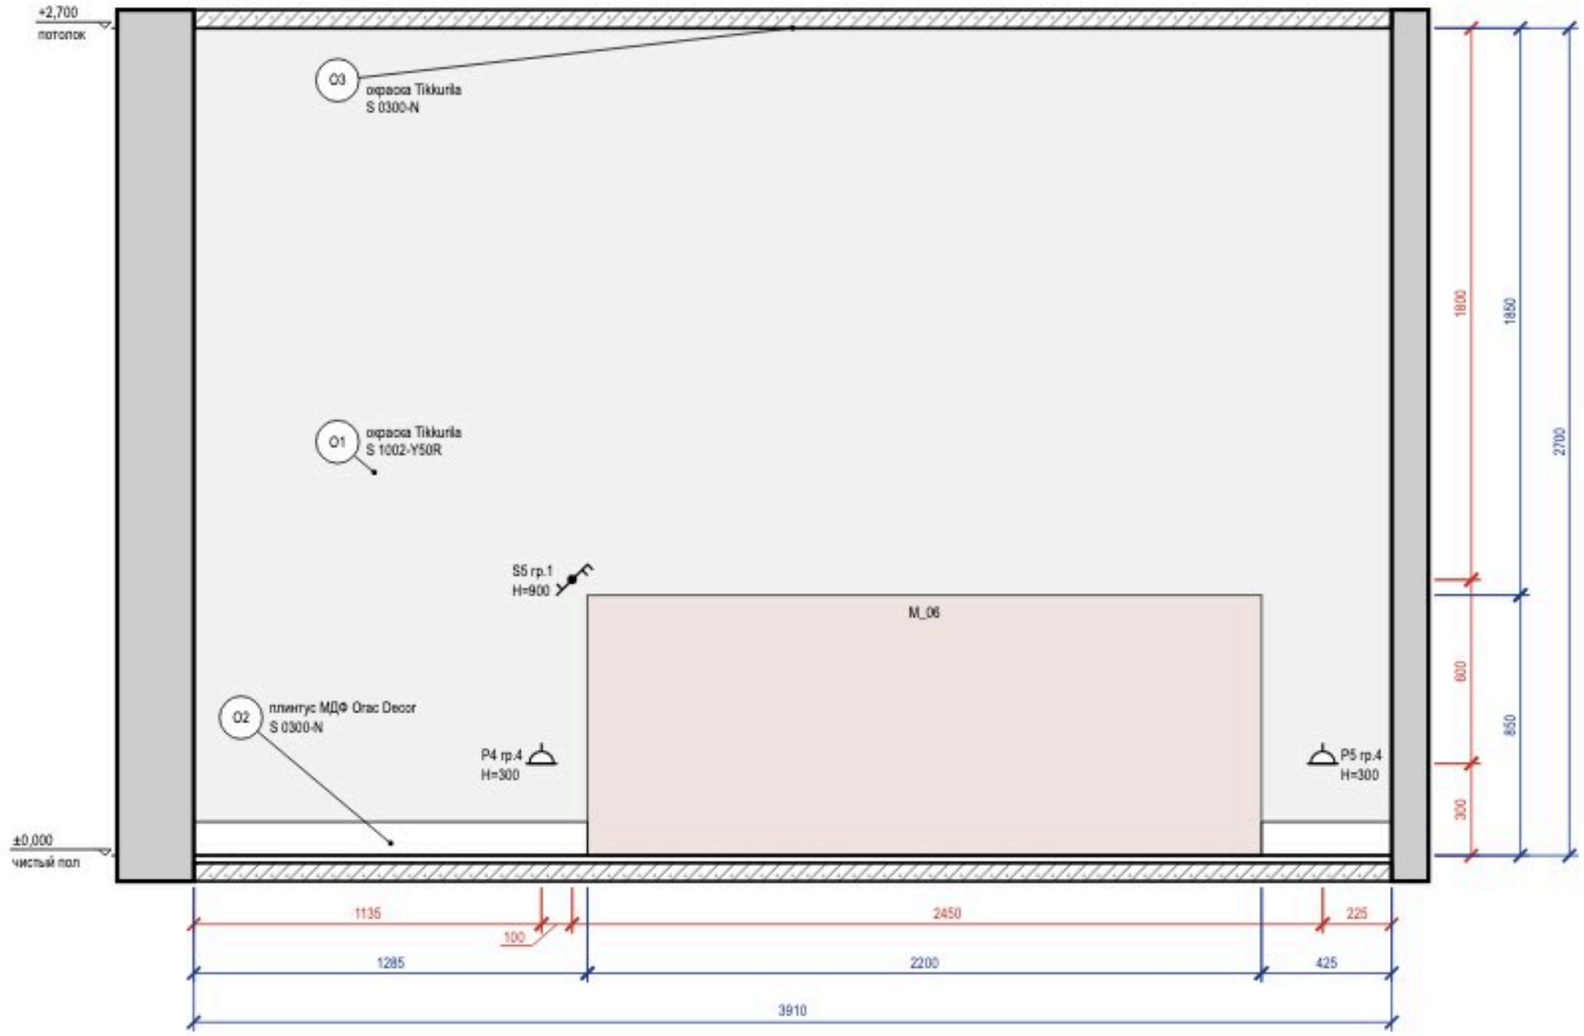


### Схема развёрток (М 1:100)

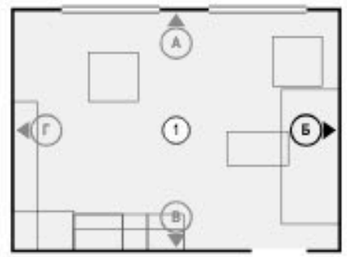


### Ведомость отделки (на листе)

| Марка | Поверхность | Материал, изделие | Цвет, код | Кол. |
|---|---|---|---|---|
| О1 | стены | окраска, Tikkurila, шелковисто-матовая, подготовка О3 | NCS S 1002-Y50R | 10,6 м² |
| О2 | плинтус | плинтус МДФ, Orac Decor Luxxus, h 110 мм, SX184, шелковисто-матовая | NCS S 0300-N | 1,7 м |
| О3 | потолок | окраска, Tikkurila, глубокоматовая | NCS S 0300-N | 21 м² |

Визуализация этой стены — лист 27



### Примечания


1. Размеры — в мм от чистовых поверхностей стен; условные обозначения и общие указания — лист 2.

| | | | | | |
|---|---|---|---|---|---|
| | | | | | Проект: Квартира 58 м² |
| | Лист | № док. | Подпись | Дата | Развёртка стены Б. Кухня-гостиная (пом. 1) |
| Дизайнер | Кырпан А.С. | | | 09.10.26 | |


| Стадия | Лист | Листов |
|---|---|---|
| П | 32 | 60 |

выпуск 09.10.2026 № 6e771c53bc · стр. 32 из 60

## Развёртка стены Г

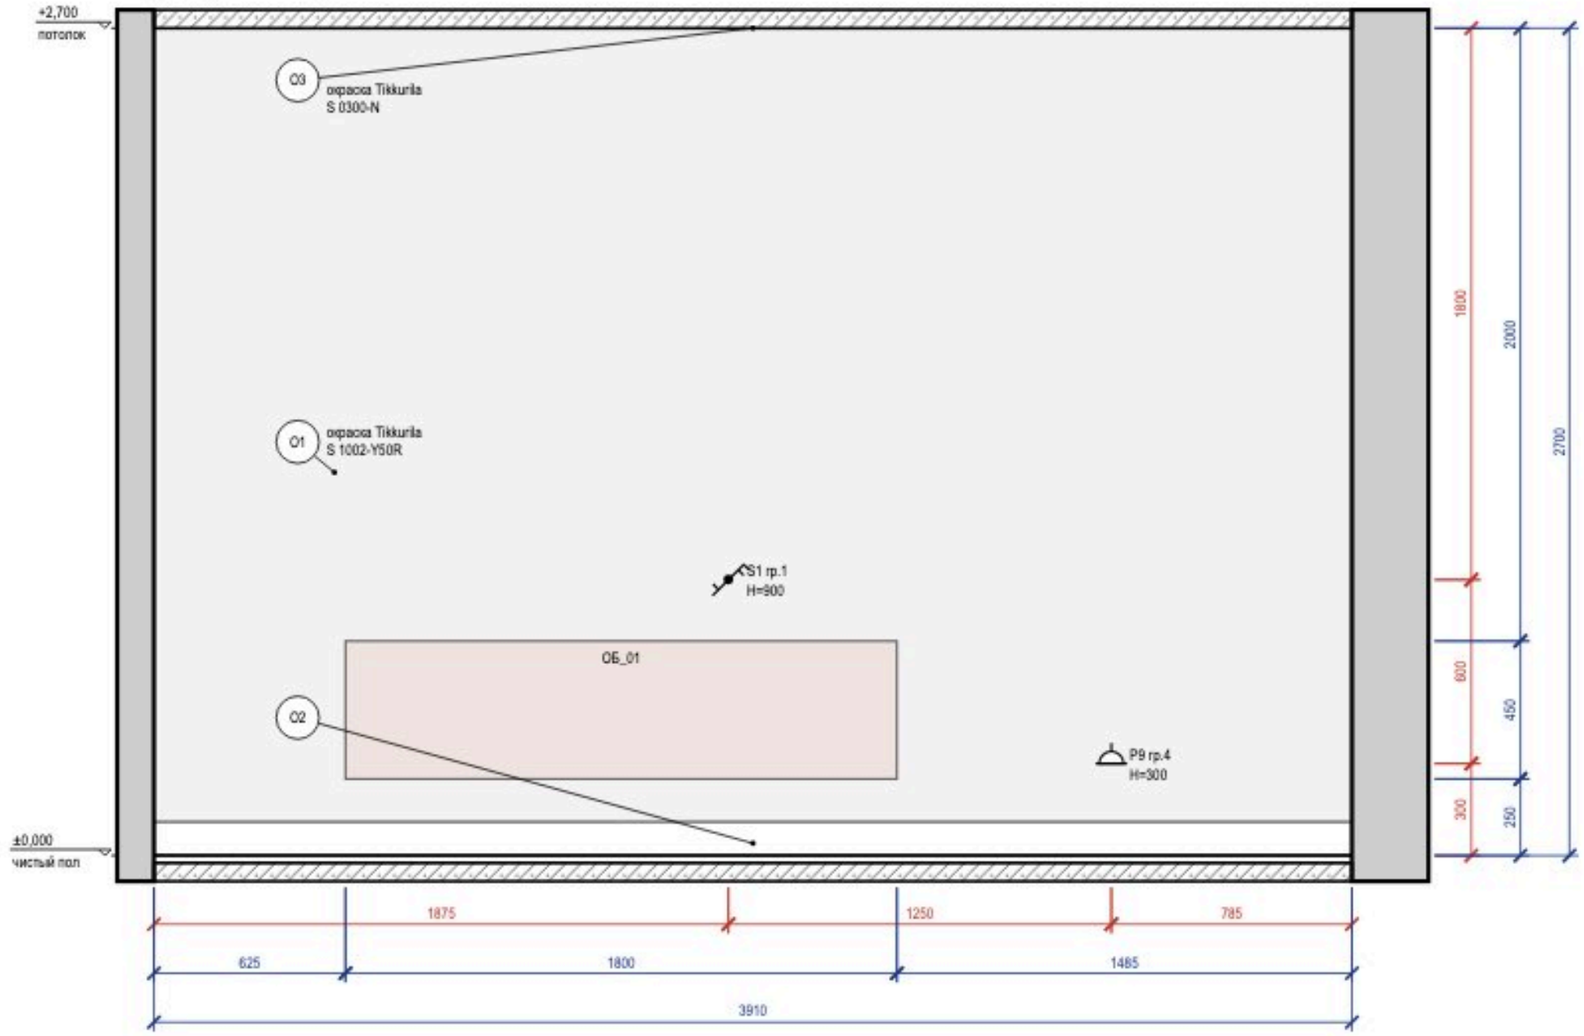


## Схема развёрток (М 1:100)

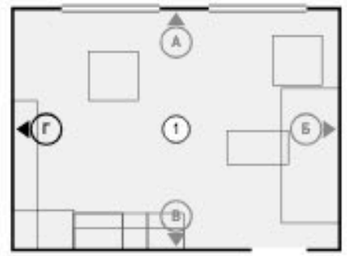


## Ведомость отделки (на листе)

| Марка | Поверхность | Материал, изделие | Цвет, код | Кол. |
|---|---|---|---|---|
| О1 | стены | окраска, Tikkurila, шелковисто-матовая, подготовка О3 | NCS S 1002-Y50R | 10,6 м² |
| О2 | плинтус | плинтус МДФ, Orac Decor Luxxus, h 110 мм, SX184, шелковисто-матовая | NCS S 0300-N | 3,9 м |
| О3 | потолок | окраска, Tikkurila, глубокоматовая | NCS S 0300-N | 21 м² |

Визуализация этой стены — лист 29



**Примечания**

1. Размеры — в мм от чистовых поверхностей стен; условные обозначения и общие указания — лист 2.

| | | | | | |
|---|---|---|---|---|---|
| | | | | | Проект: Квартира 58 м² |
| | Лист | № док. | Подпись | Дата | Развёртка стены Г. Кухня-гостиная (пом. 1) |
| Дизайнер | Кырпан А.С. | | | 09.10.26 | |

| Стадия | Лист | Листов |
|---|---|---|
| П | 33 | 60 |

выпуск 09.10.2026 № 6e771c53bc · стр. 33 из 60



| | | | | | | |
|---|---|---|---|---|---|---|
| | | | | | Проект: Квартира 58 м² | |
| | Лист | № док. | Подпись | Дата | Визуализация спальни | Стадия / Лист / Листов |
| Дизайнер | Кырпан А.С. | | | 09.10.26 | | П / 34 / 60 |


выпуск 09.10.2026 № 6e771c53bc · стр. 34 из 60




| | | | | | | |
|---|---|---|---|---|---|---|
| | | | | | Проект: Квартира 58 м² | |
| | Лист | № док. | Подпись | Дата | Визуализация спальни | Стадия / Лист / Листов |
| Дизайнер | Кырпан А.С. | | | 09.10.26 | | П / 35 / 60 |

выпуск 09.10.2026 № 6e771c53bc · стр. 35 из 60

## Развёртка стены А

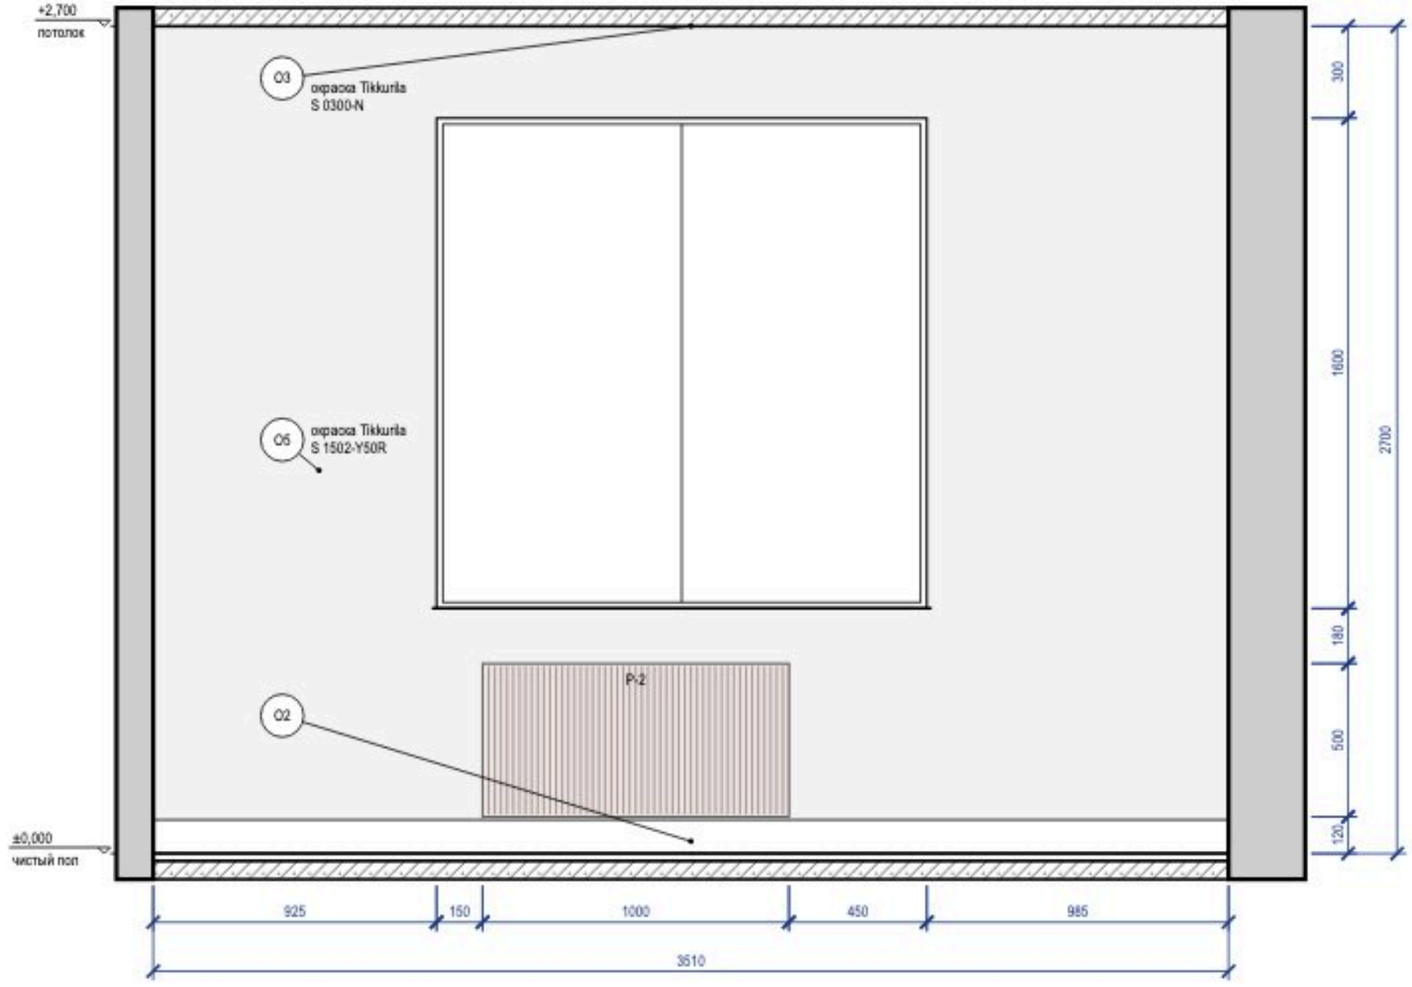



## Схема развёрток (М 1:100)

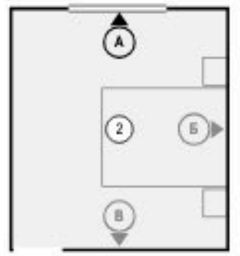


## Ведомость отделки (на листе)

| Марка | Поверхность | Материал, изделие | Цвет, код | Кол. |
|---|---|---|---|---|
| О2 | плинтус | плинтус МДФ, Orac Decor Luxxus, h 110 мм, SX184, шелковисто-матовая | NCS S 0300-N | 3,5 м |
| О3 | потолок | окраска, Tikkurila, глубокоматовая | NCS S 0300-N | 13,9 м² |
| О5 | стены | окраска, Tikkurila, глубокоматовая, подготовка Q3 | NCS S 1502-Y50R | 6,9 м² |

Визуализация этой стены — лист 34

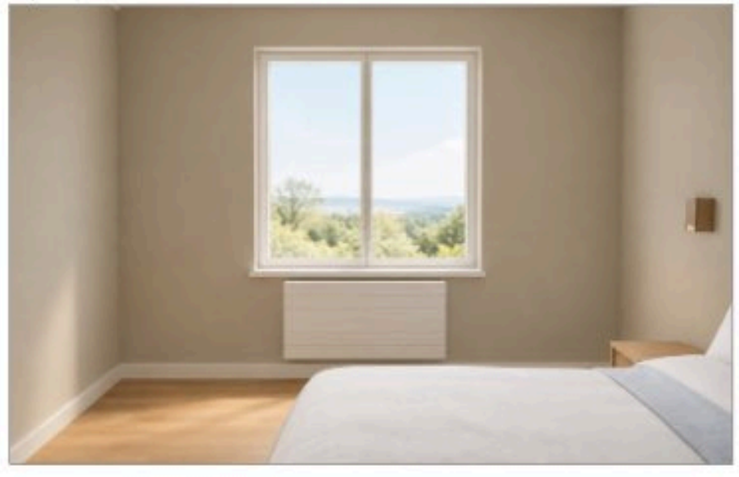

### Примечания


1. Размеры — в мм от чистовых поверхностей стен; условные обозначения и общие указания — лист 2.

| | | | | | |
|---|---|---|---|---|---|
| | Лист | № док. | Подпись | Дата | Проект: Квартира 58 м² |
| Дизайнер | Кырпан А.С. | | | 09.10.26 | Развёртка стены А. Спальня (пом. 2) |


| Стадия | Лист | Листов |
|---|---|---|
| П | 36 | 60 |

выпуск 09.10.2026 № 6e771c53bc · стр. 36 из 60

## Развёртка стены Б

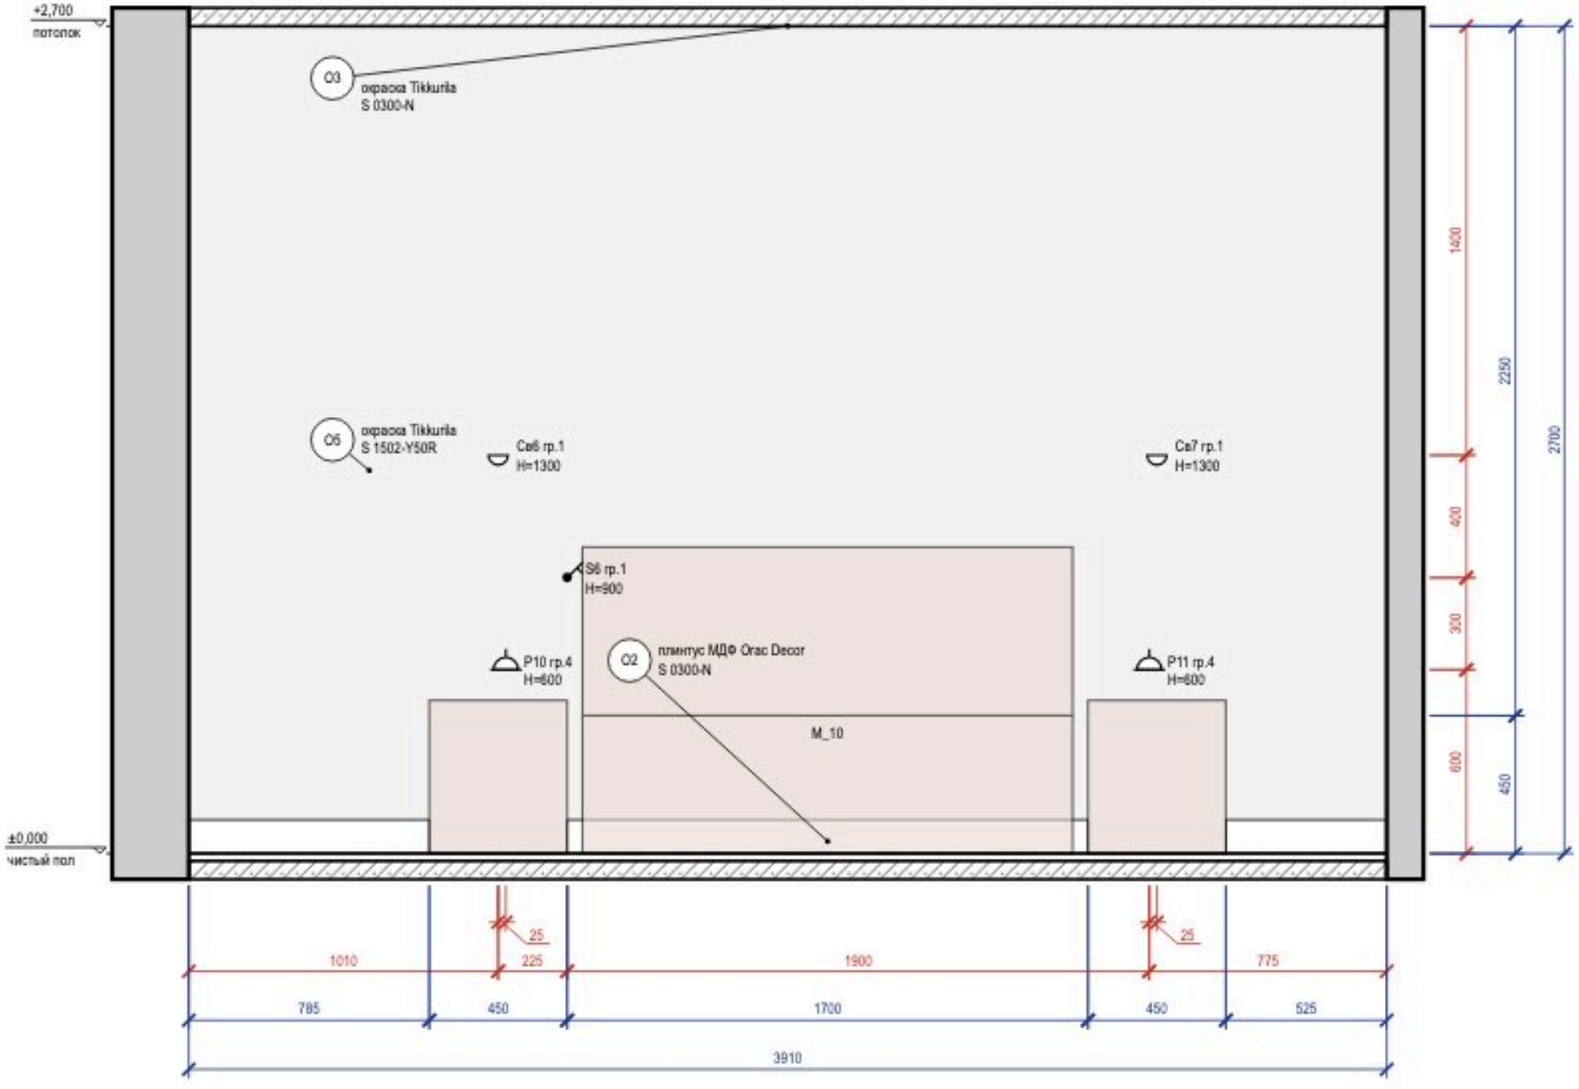



## Схема развёрток (М 1:100)

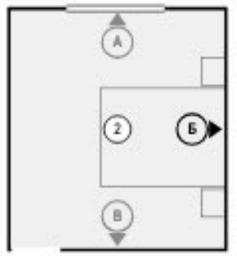


## Ведомость отделки (на листе)

| Марка | Поверхность | Материал, изделие | Цвет, код | Кол. |
|---|---|---|---|---|
| О2 | плинтус | плинтус МДФ, Orac Decor Luxxus, h 110 мм, SX184, шелковисто-матовая | NCS S 0300-N | 3 м |
| О3 | потолок | окраска, Tikkurila, глубокоматовая | NCS S 0300-N | 13,9 м² |
| О5 | стены | окраска, Tikkurila, глубокоматовая, подготовка Q3 | NCS S 1502-Y50R | 10,6 м² |

Визуализация этой стены — лист 35

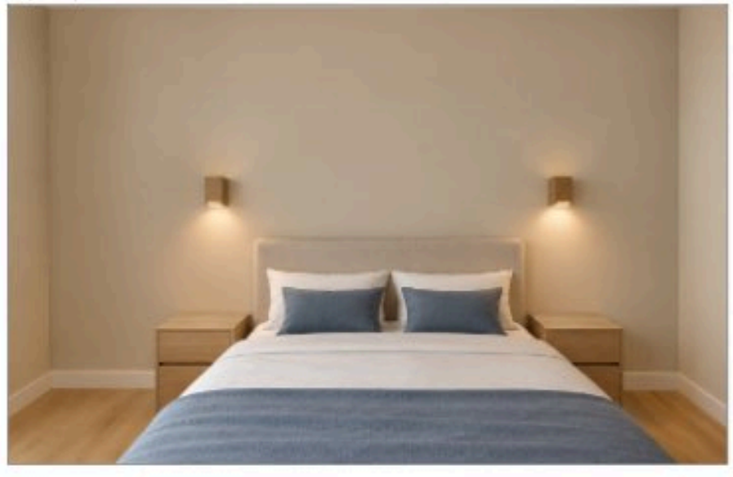

### Примечания


1. Размеры — в мм от чистовых поверхностей стен; условные обозначения и общие указания — лист 2.

| | | | | | |
|---|---|---|---|---|---|
| | Лист | № док. | Подпись | Дата | Проект: Квартира 58 м² |
| Дизайнер | Кырпан А.С. | | | 09.10.26 | Развёртка стены Б. Спальня (пом. 2) |


| Стадия | Лист | Листов |
|---|---|---|
| П | 37 | 60 |

выпуск 09.10.2026 · 6e771c53bc · стр. 37 из 60

## Развёртка стены В

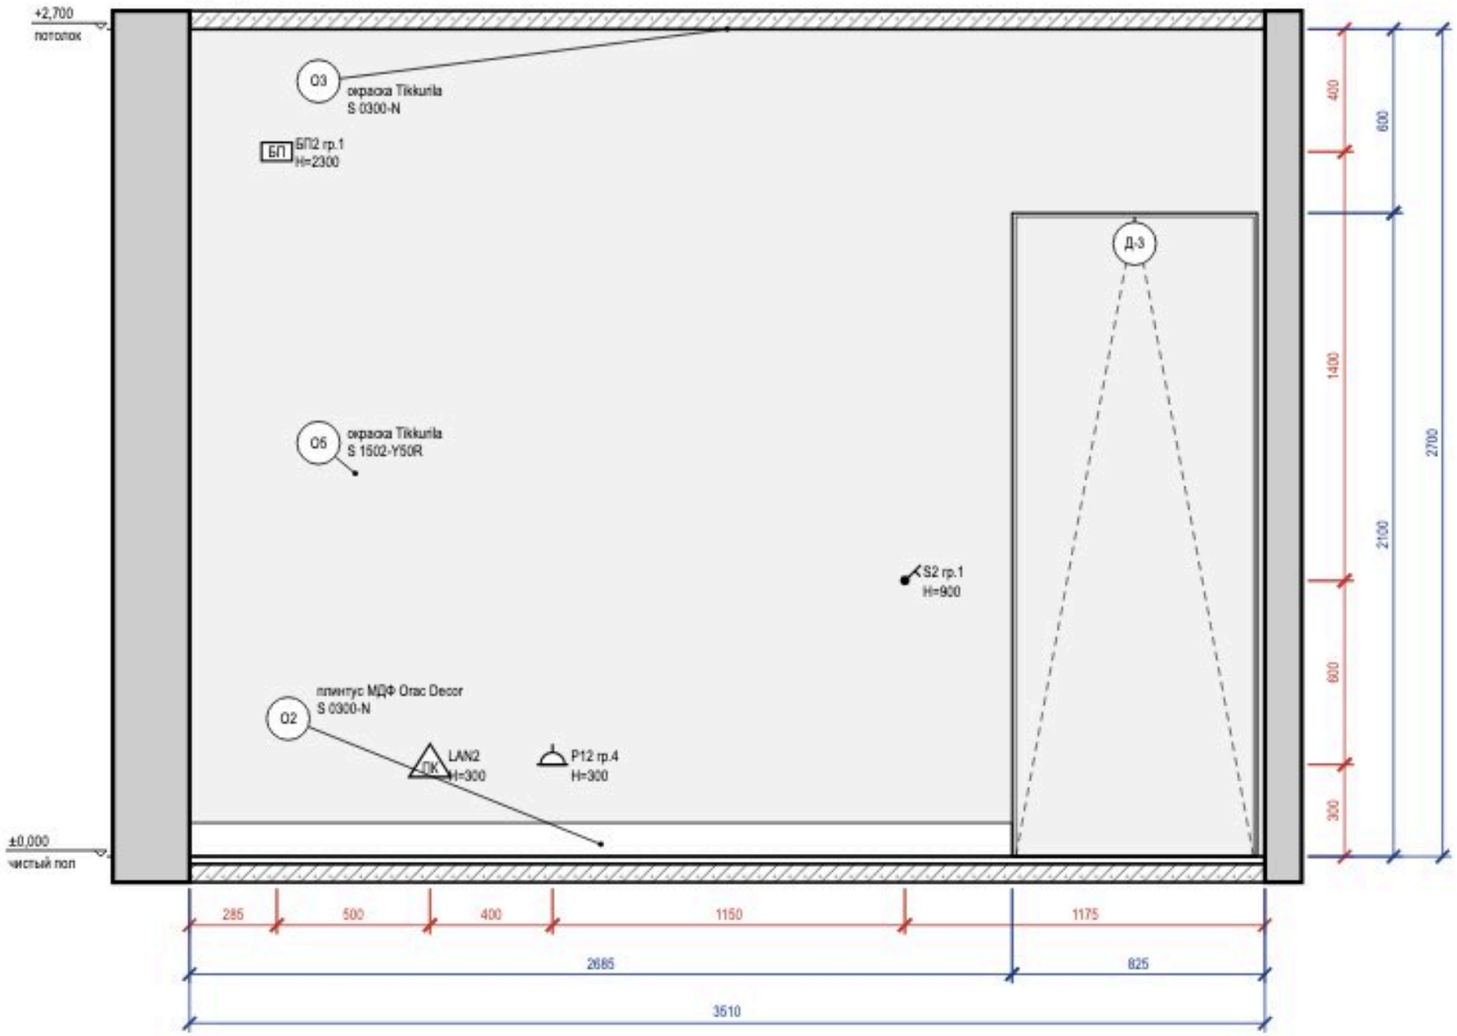


## Схема развёрток (М 1:100)

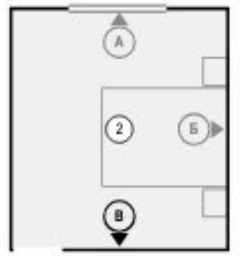



## Ведомость отделки (на листе)

| Марка | Поверхность | Материал, изделие | Цвет, код | Кол. |
|---|---|---|---|---|
| О2 | плинтус | плинтус МДФ, Orac Decor Luxxus, h 110 мм, SX184, шелковисто-матовая | NCS S 0300-N | 2,7 м |
| О3 | потолок | окраска, Tikkurila, глубокоматовая | NCS S 0300-N | 13,9 м² |
| О5 | стены | окраска, Tikkurila, глубокоматовая, подготовка Q3 | NCS S 1502-Y50R | 7,8 м² |

## 5 Плинтус МДФ 110×16 мм у окрашенной стены (М 1:10)

Узел 5 — лист С3

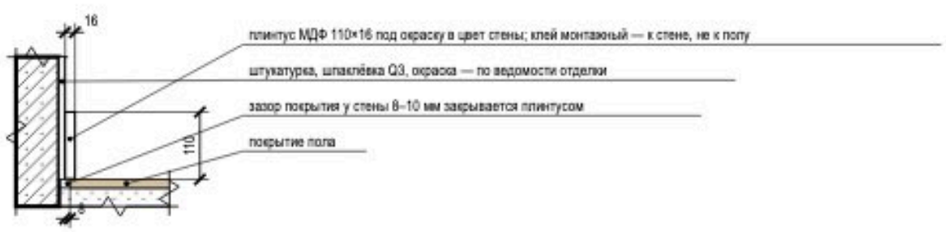


## Примечания

1. Размеры — в мм от чистовых поверхностей стен; условные обозначения и общие указания — лист 2.
2. Двери скрытого монтажа — полотно в плоскости стены, отделка стены по полотну, плинтус прерывается у короба (узел — на листе узлов).

| | | | | | Проект: Квартира 58 м² | | | |
|---|---|---|---|---|---|---|---|---|
| | Лист | № док. | Подпись | Дата | Развёртка стены В. Спальня (пом. 2) | Стадия | Лист | Листов |
| Дизайнер | Кырпан А.С. | | | 09.10.26 | | П | 38 | 60 |

выпуск 09.10.2026 № 6e771c53bc · стр. 38 из 60



| | | | | | | |
|---|---|---|---|---|---|---|
| | | | | | Проект: Квартира 58 м² | |
| | Лист | № док. | Подпись | Дата | Визуализация ванной | Стадия / Лист / Листов |
| Дизайнер | Кырпан А.С. | | | 09.10.26 | | П / 39 / 60 |


выпуск 09.10.2026 № 6e771c53bc · стр. 39 из 60




| | | | | | Проект: Квартира 58 м² | | | |
|---|---|---|---|---|---|---|---|---|
| | Лист | № док. | Подпись | Дата | Визуализация ванной | Стадия | Лист | Листов |
| Дизайнер | Кырпан А.С. | | | 09.10.26 | | П | 40 | 60 |

выпуск 09.10.2026 № 6e771c53bc · стр. 40 из 60

## Развёртка стены А

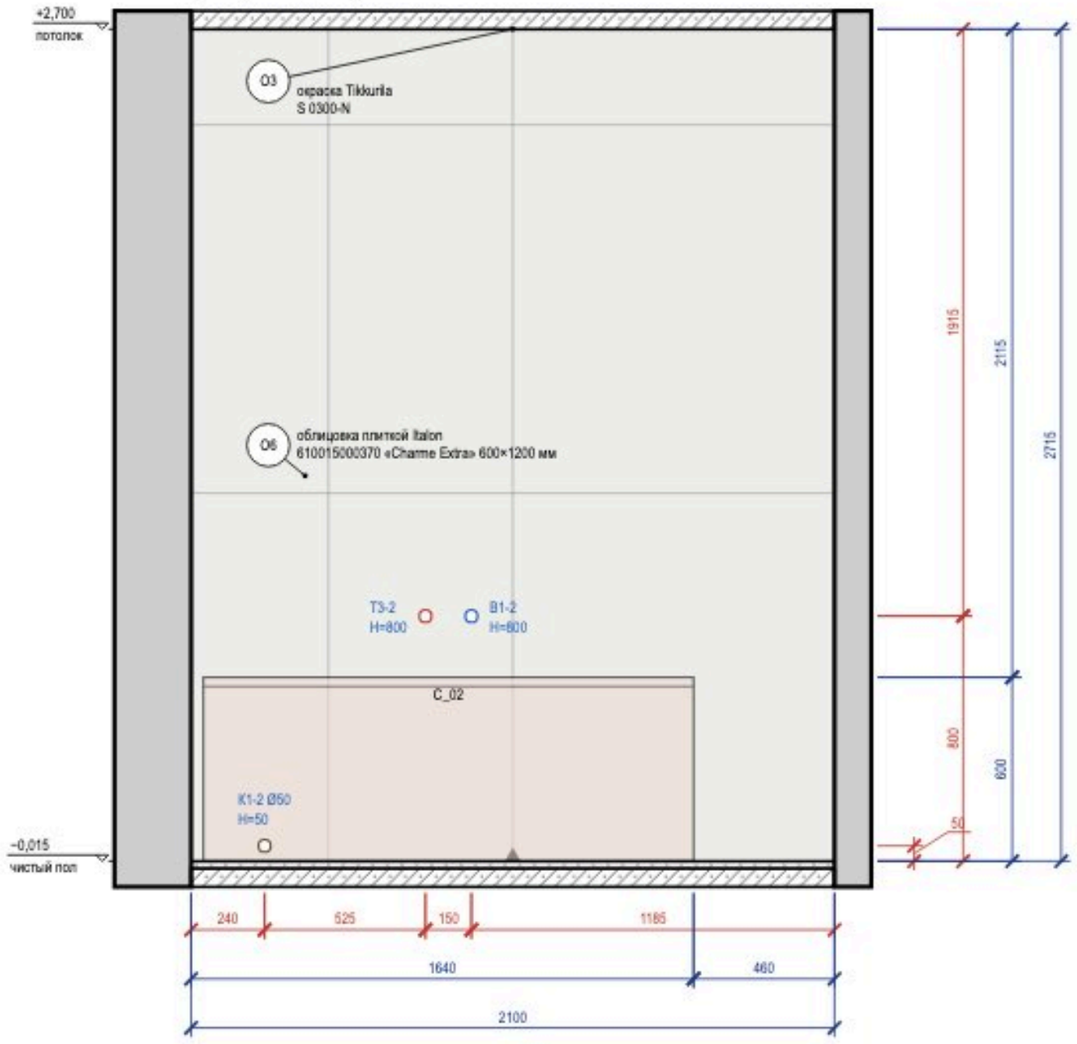


## Развёртка стены Б

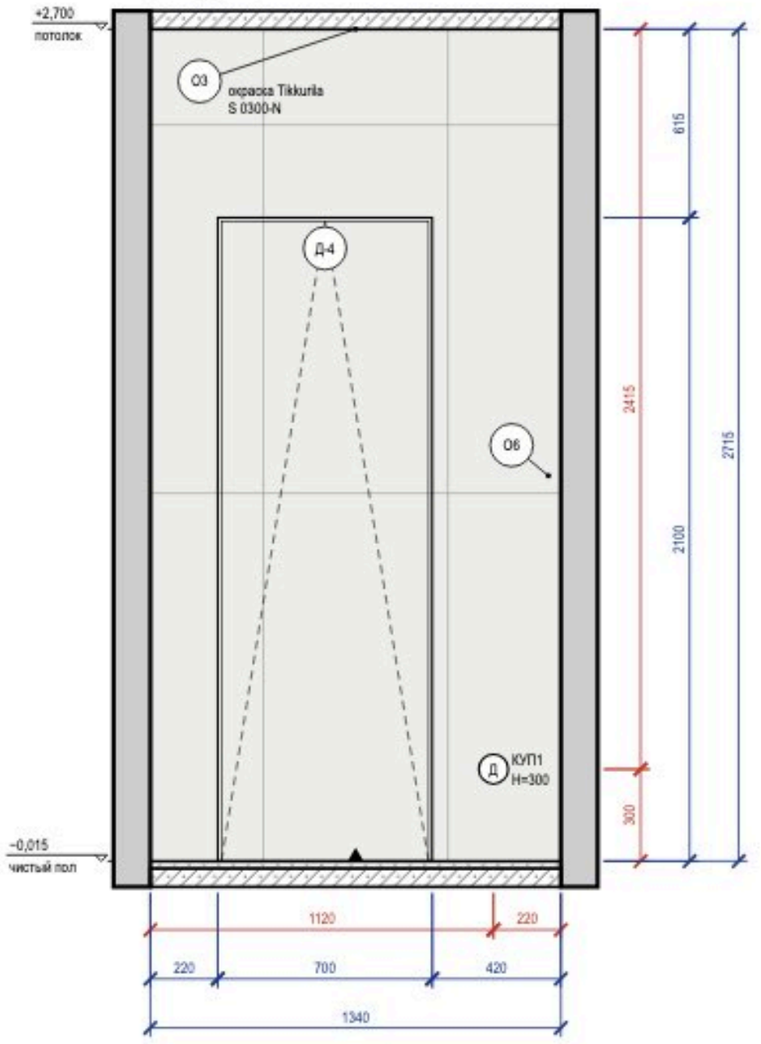



### Схема развёрток (М 1:100)




### Ведомость отделки (на листе)

| Марка | Поверхность | Материал, изделие | Цвет, код | Кол. |
|---|---|---|---|---|
| О3 | потолок | окраска, Tikkurila, глубокоматовая | NCS S 0300-N | 3 м² |
| О6 | стены | облицовка плиткой, Italon Charme Extra, 600×1200 мм, 610015000370 | Italon 610015000370 «Charme Extra» | 7,9 м² |

Визуализация этой стены — лист 39

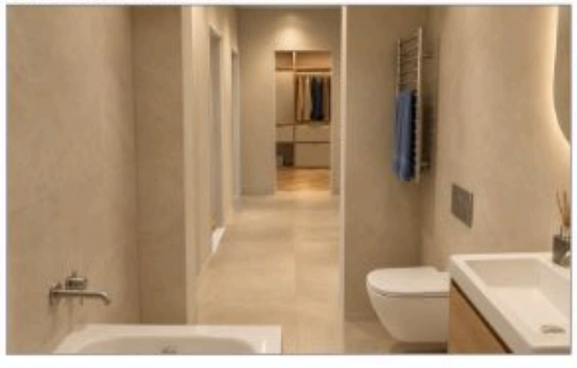

### Примечания


1. Размеры — в мм от чистовых поверхностей стен; условные обозначения и общие указания — лист 2.
2. Облицовка — по сетке швов, раскладка от оси стены (треугольник у пола); подрезки — по листу раскладки плитки.
3. Гидроизоляция в 2 слоя, заход на стены 200 мм — до облицовки, с актом скрытых работ и тестом проливом (узел — на листе узлов).
4. Двери скрытого монтажа — полотно в плоскости стены, отделка стены по полотну, плинтус прерывается у короба (узел — на листе узлов).

| | | | | | |
|---|---|---|---|---|---|
| | | | | | Проект: Квартира 58 м² |
| | Лист | № док. | Подпись | Дата | Развёртки стен А, Б. Ванная (пом. 3) |
| Дизайнер | Кырпан А.С. | | | 09.10.26 | |


| Стадия | Лист | Листов |
|---|---|---|
| П | 41 | 60 |

выпуск 09.10.2026 № 6e771c53bc · стр. 41 из 60

## Развёртка стены В

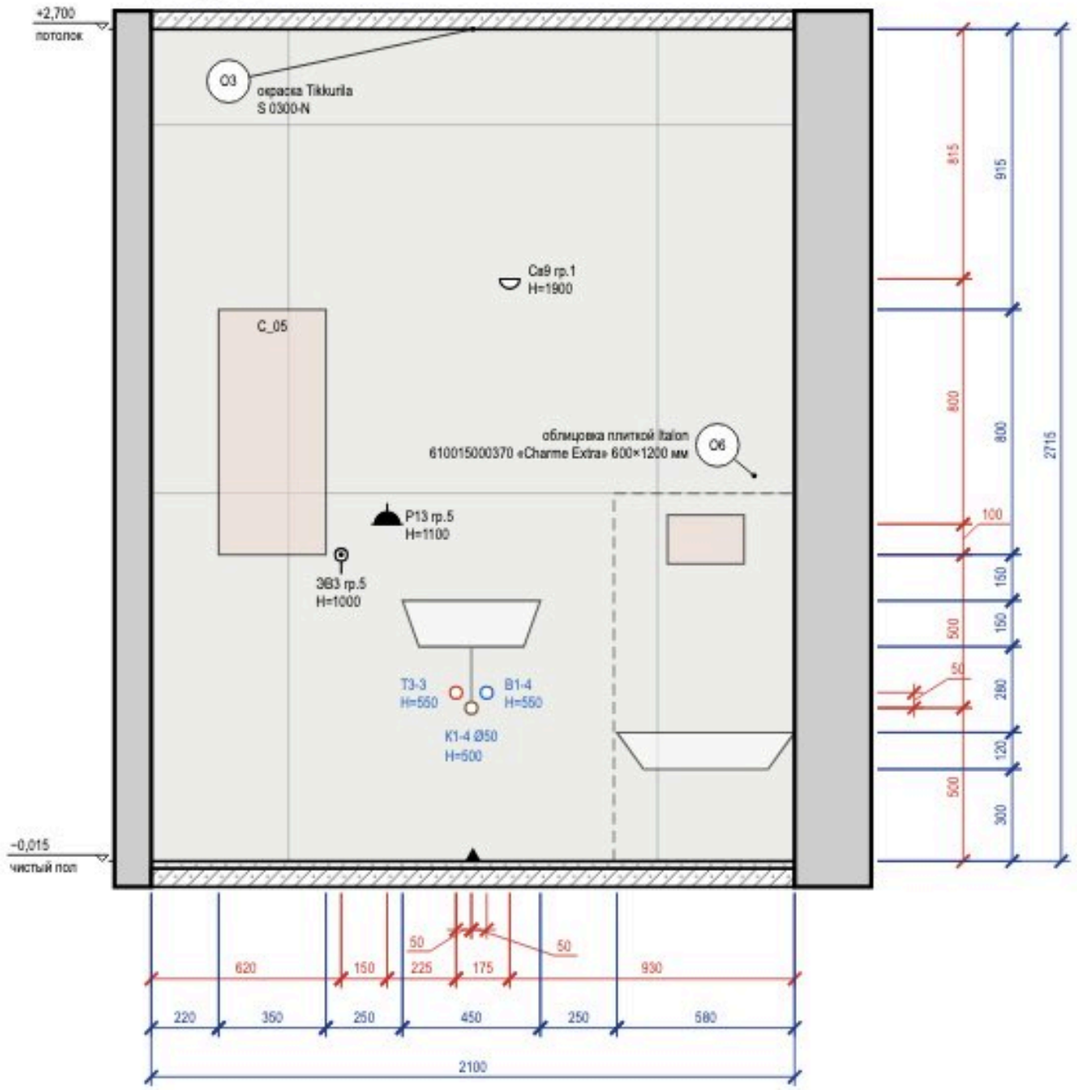


## Развёртка стены Г

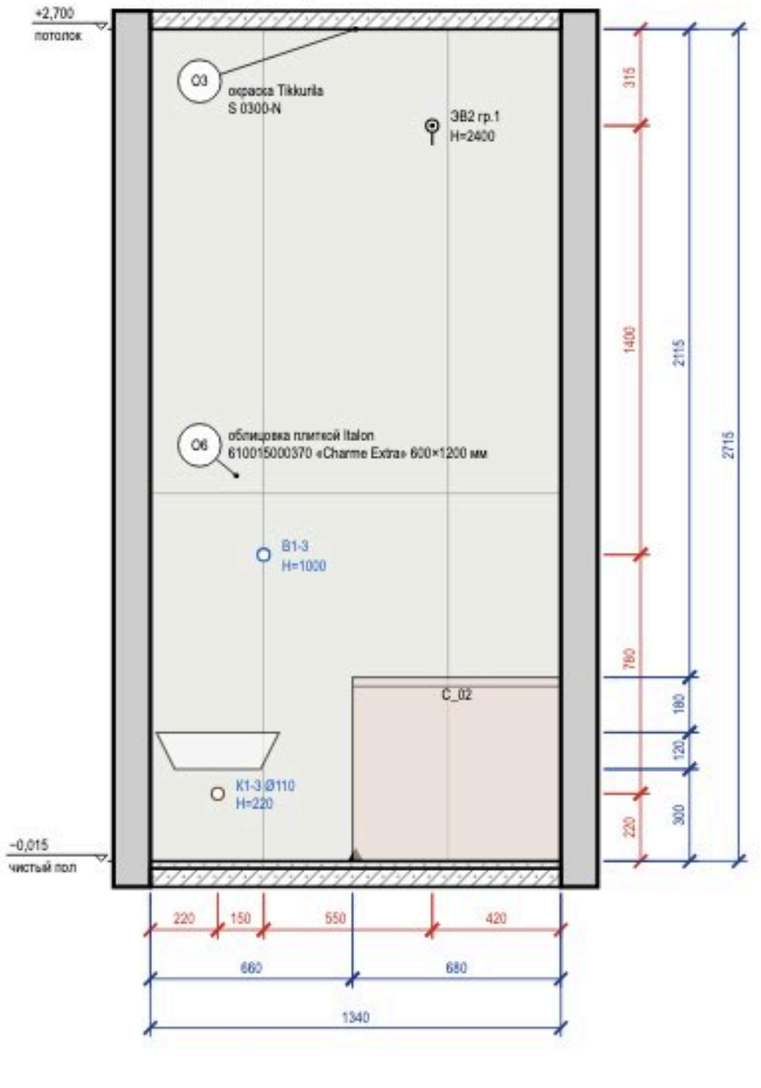



### Схема развёрток (М 1:100)




### Ведомость отделки (на листе)

| Марка | Поверхность | Материал, изделие | Цвет, код | Кол. |
|---|---|---|---|---|
| О3 | потолок | окраска, Tikkurila, глубокоматовая | NCS S 0300-N | 3 м² |
| О6 | стены | облицовка плиткой, Italon Charme Extra, 600×1200 мм, 610015000370 | Italon 610015000370 «Charme Extra» | 9,3 м² |

Визуализация этой стены — лист 40

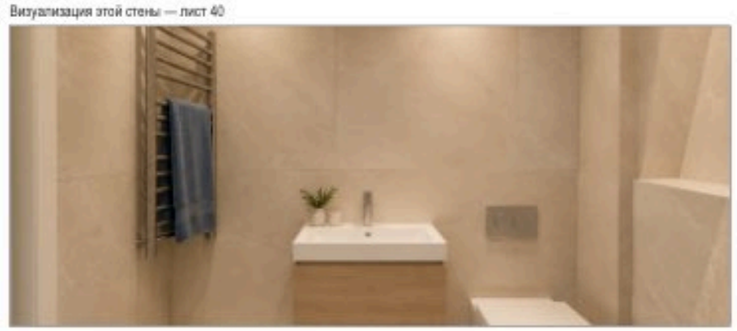

### Примечания

1. Размеры — в мм от чистовых поверхностей стен; условные обозначения и общие указания — лист 2.
2. Схема мебели, приборов и декора не является технической документацией для производства мебели; габариты — по паспортам изделий.
3. Облицовка — по сетке швов, раскладка от оси стены (треугольник у пола); подрезки — по листу раскладки плитки.
4. Гидроизоляция в 2 слоя, заход на стены 200 мм — до облицовки, с актом скрытых работ и тестом проливом (узел — на листе узлов).

| | | | | | |
|---|---|---|---|---|---|
| | | | | | Проект: Квартира 58 м² |
| | Лист | № док. | Подпись | Дата | Развёртки стен В, Г. Ванная (пом. 3) |
| Дизайнер | Кырпан А.С. | | | 09.10.26 | |

| Стадия | Лист | Листов |
|---|---|---|
| П | 42 | 60 |


выпуск 09.10.2026 № 6e771c53bc · стр. 42 из 60




| | | | | | | |
|---|---|---|---|---|---|---|
| | | | | | Проект: Квартира 58 м² | |
| | Лист | № док. | Подпись | Дата | Визуализация санузла | Стадия / Лист / Листов |
| Дизайнер | Кырпан А.С. | | | 09.10.26 | | П / 43 / 60 |

выпуск 09.10.2026 № 6e771c53bc · стр. 43 из 60

## Развёртка стены А

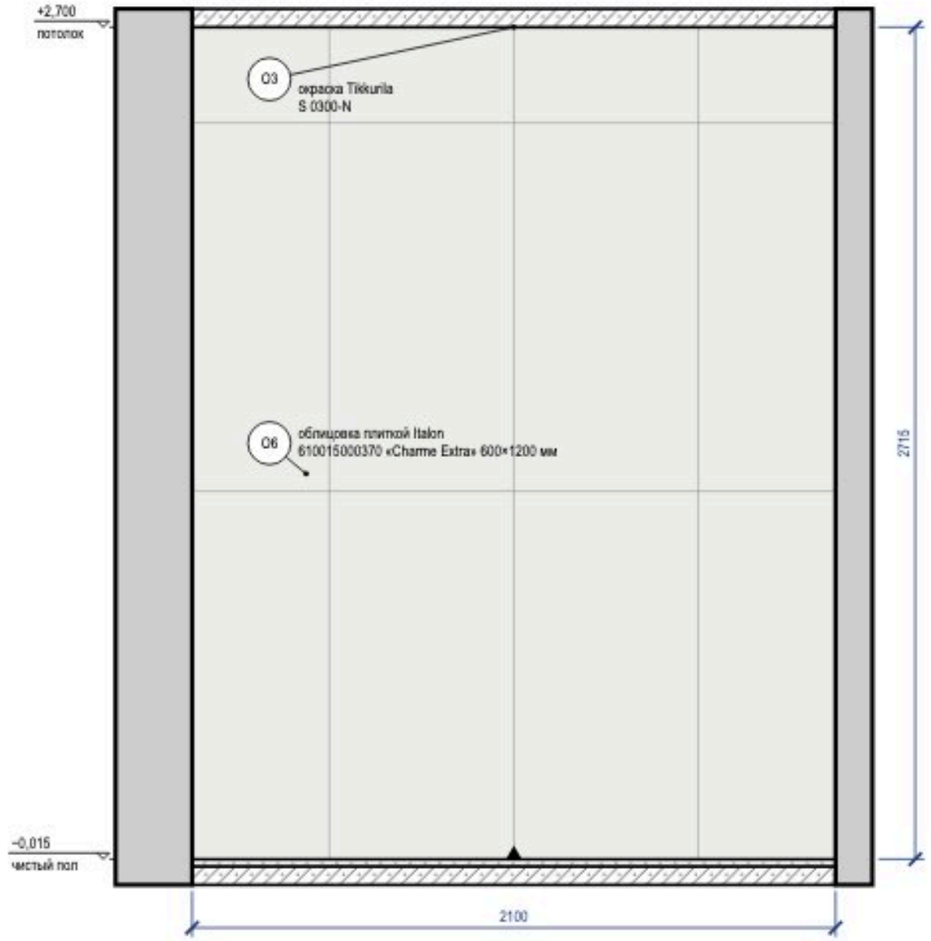


## Развёртка стены Б

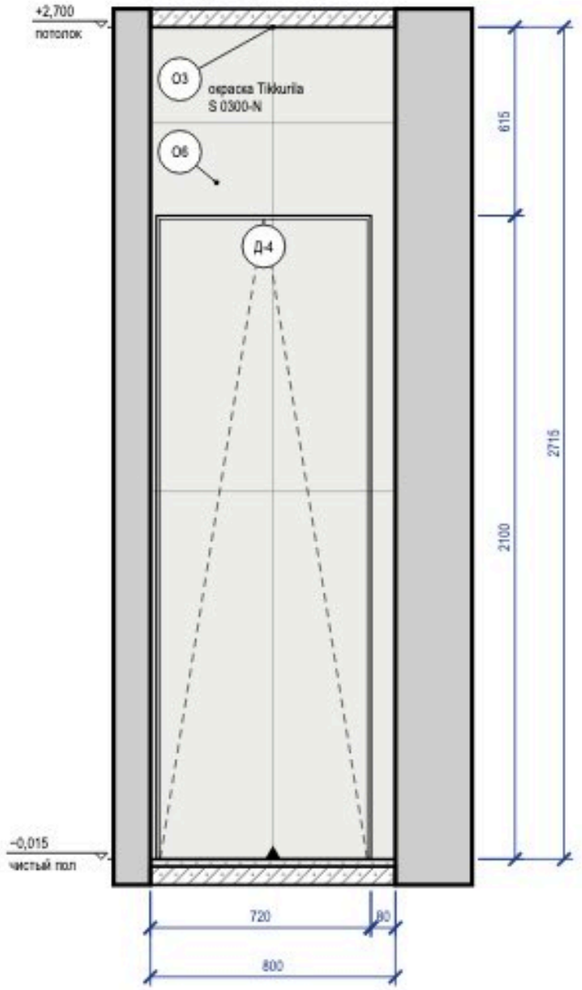


## Схема развёрток (М 1:100)




## Ведомость отделки (на листе)

| Марка | Поверхность | Материал, изделие | Цвет, код | Кол. |
|---|---|---|---|---|
| О3 | потолок | окраска, Tikkurila, глубокоматовая | NCS S 0300-N | 1,8 м² |
| О6 | стены | облицовка плиткой, Italon Charme Extra, 600×1200 мм, 610015000370 | Italon 610015000370 «Charme Extra» | 6,4 м² |

## Примечания


1. Размеры — в мм от чистовых поверхностей стен; условные обозначения и общие указания — лист 2.
2. Облицовка — по сетке швов, раскладка от оси стены (треугольник у пола); подрезки — по листу раскладки плитки.
3. Гидроизоляция в 2 слоя, заход на стены 200 мм — до облицовки, с актом скрытых работ и тестом проливом (узел — на листе узлов).
4. Двери скрытого монтажа — полотно в плоскости стены, отделка стены по полотну, плинтус прерывается у короба (узел — на листе узлов).

| | | | | | |
|---|---|---|---|---|---|
| | | | | | Проект: Квартира 58 м² |
| | Лист | № док. | Подпись | Дата | Развёртки стен А, Б. Санузел (пом. 4) |
| Дизайнер | Кырпан А.С. | | | 09.10.26 | |


| Стадия | Лист | Листов |
|---|---|---|
| П | 44 | 60 |

выпуск 09.10.2026 № 6e771c53bc · стр. 44 из 60

## Развёртка стены В

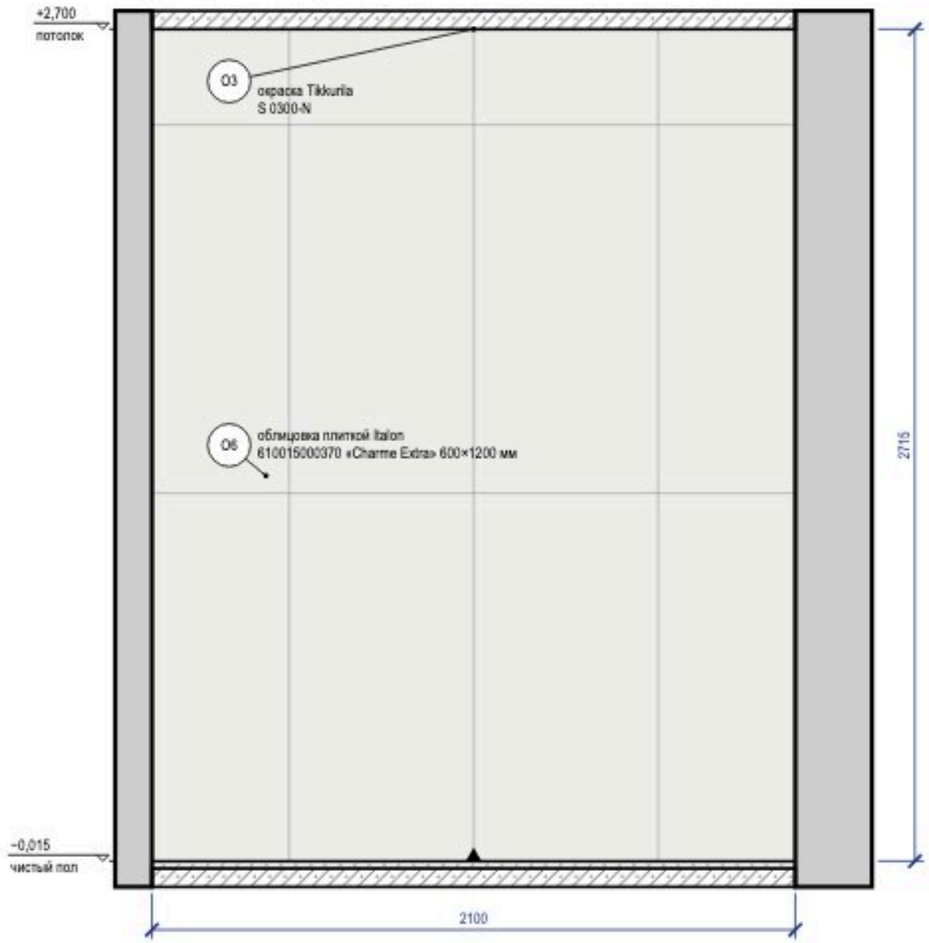


## Развёртка стены Г

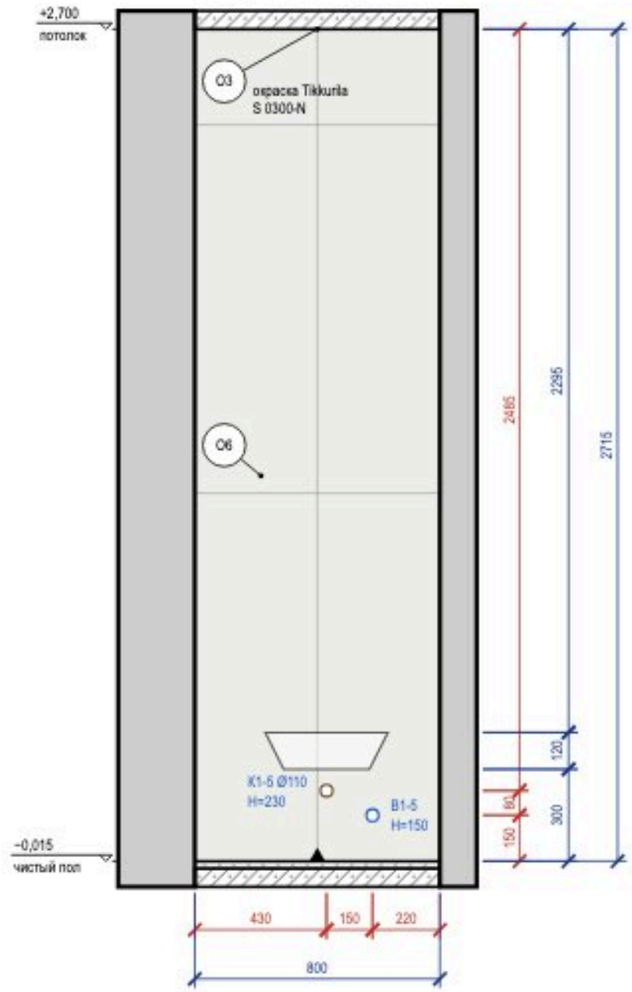



## Схема развёрток (М 1:100)




## Ведомость отделки (на листе)

| Марка | Поверхность | Материал, изделие | Цвет, код | Кол. |
|---|---|---|---|---|
| О3 | потолок | окраска, Tikkurila, глубокоматовая | NCS S 0300-N | 1,8 м² |
| О6 | стены | облицовка плиткой, Italon Charme Extra, 600×1200 мм, 610015000370 | Italon 610015000370 «Charme Extra» | 7,9 м² |

Визуализация этой стены — лист 43

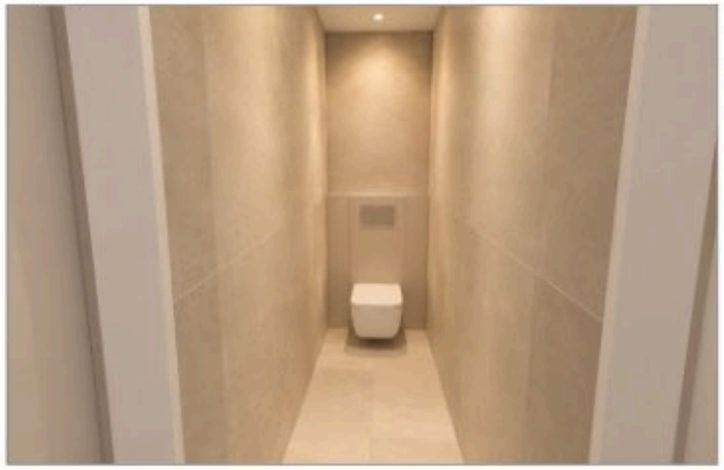

## Примечания

1. Размеры — в мм от чистовых поверхностей стен; условные обозначения и общие указания — лист 2.
2. Схема мебели, приборов и декора не является технической документацией для производства мебели; габариты — по паспортам изделий.
3. Облицовка — по сетке швов, раскладка от оси стены (треугольник у пола); подрезки — по листу раскладки плитки.
4. Гидроизоляция в 2 слоя, заход на стены 200 мм — до облицовки, с актом скрытых работ и тестом проливом (узел — на листе узлов).

| | | | | | |
|---|---|---|---|---|---|
| | | | | | Проект: Квартира 58 м² |
| | Лист | № док. | Подпись | Дата | Развёртки стен В, Г. Санузел (пом. 4) |
| Дизайнер | Кырпан А.С. | | | 09.10.26 | |

| Стадия | Лист | Листов |
|---|---|---|
| П | 45 | 60 |


выпуск 09.10.2026 № 6e771c53bc · стр. 45 из 60



| | | | | | |
|---|---|---|---|---|---|
| | | | | | Проект: Квартира 58 м² |
| | Лист | № док. | Подпись | Дата | |
| Дизайнер | Кырпан А.С. | | | 09.10.26 | Визуализация прихожей |

| Стадия | Лист | Листов |
|---|---|---|
| П | 46 | 60 |


выпуск 09.10.2026 № 6e771c53bc · стр. 46 из 60

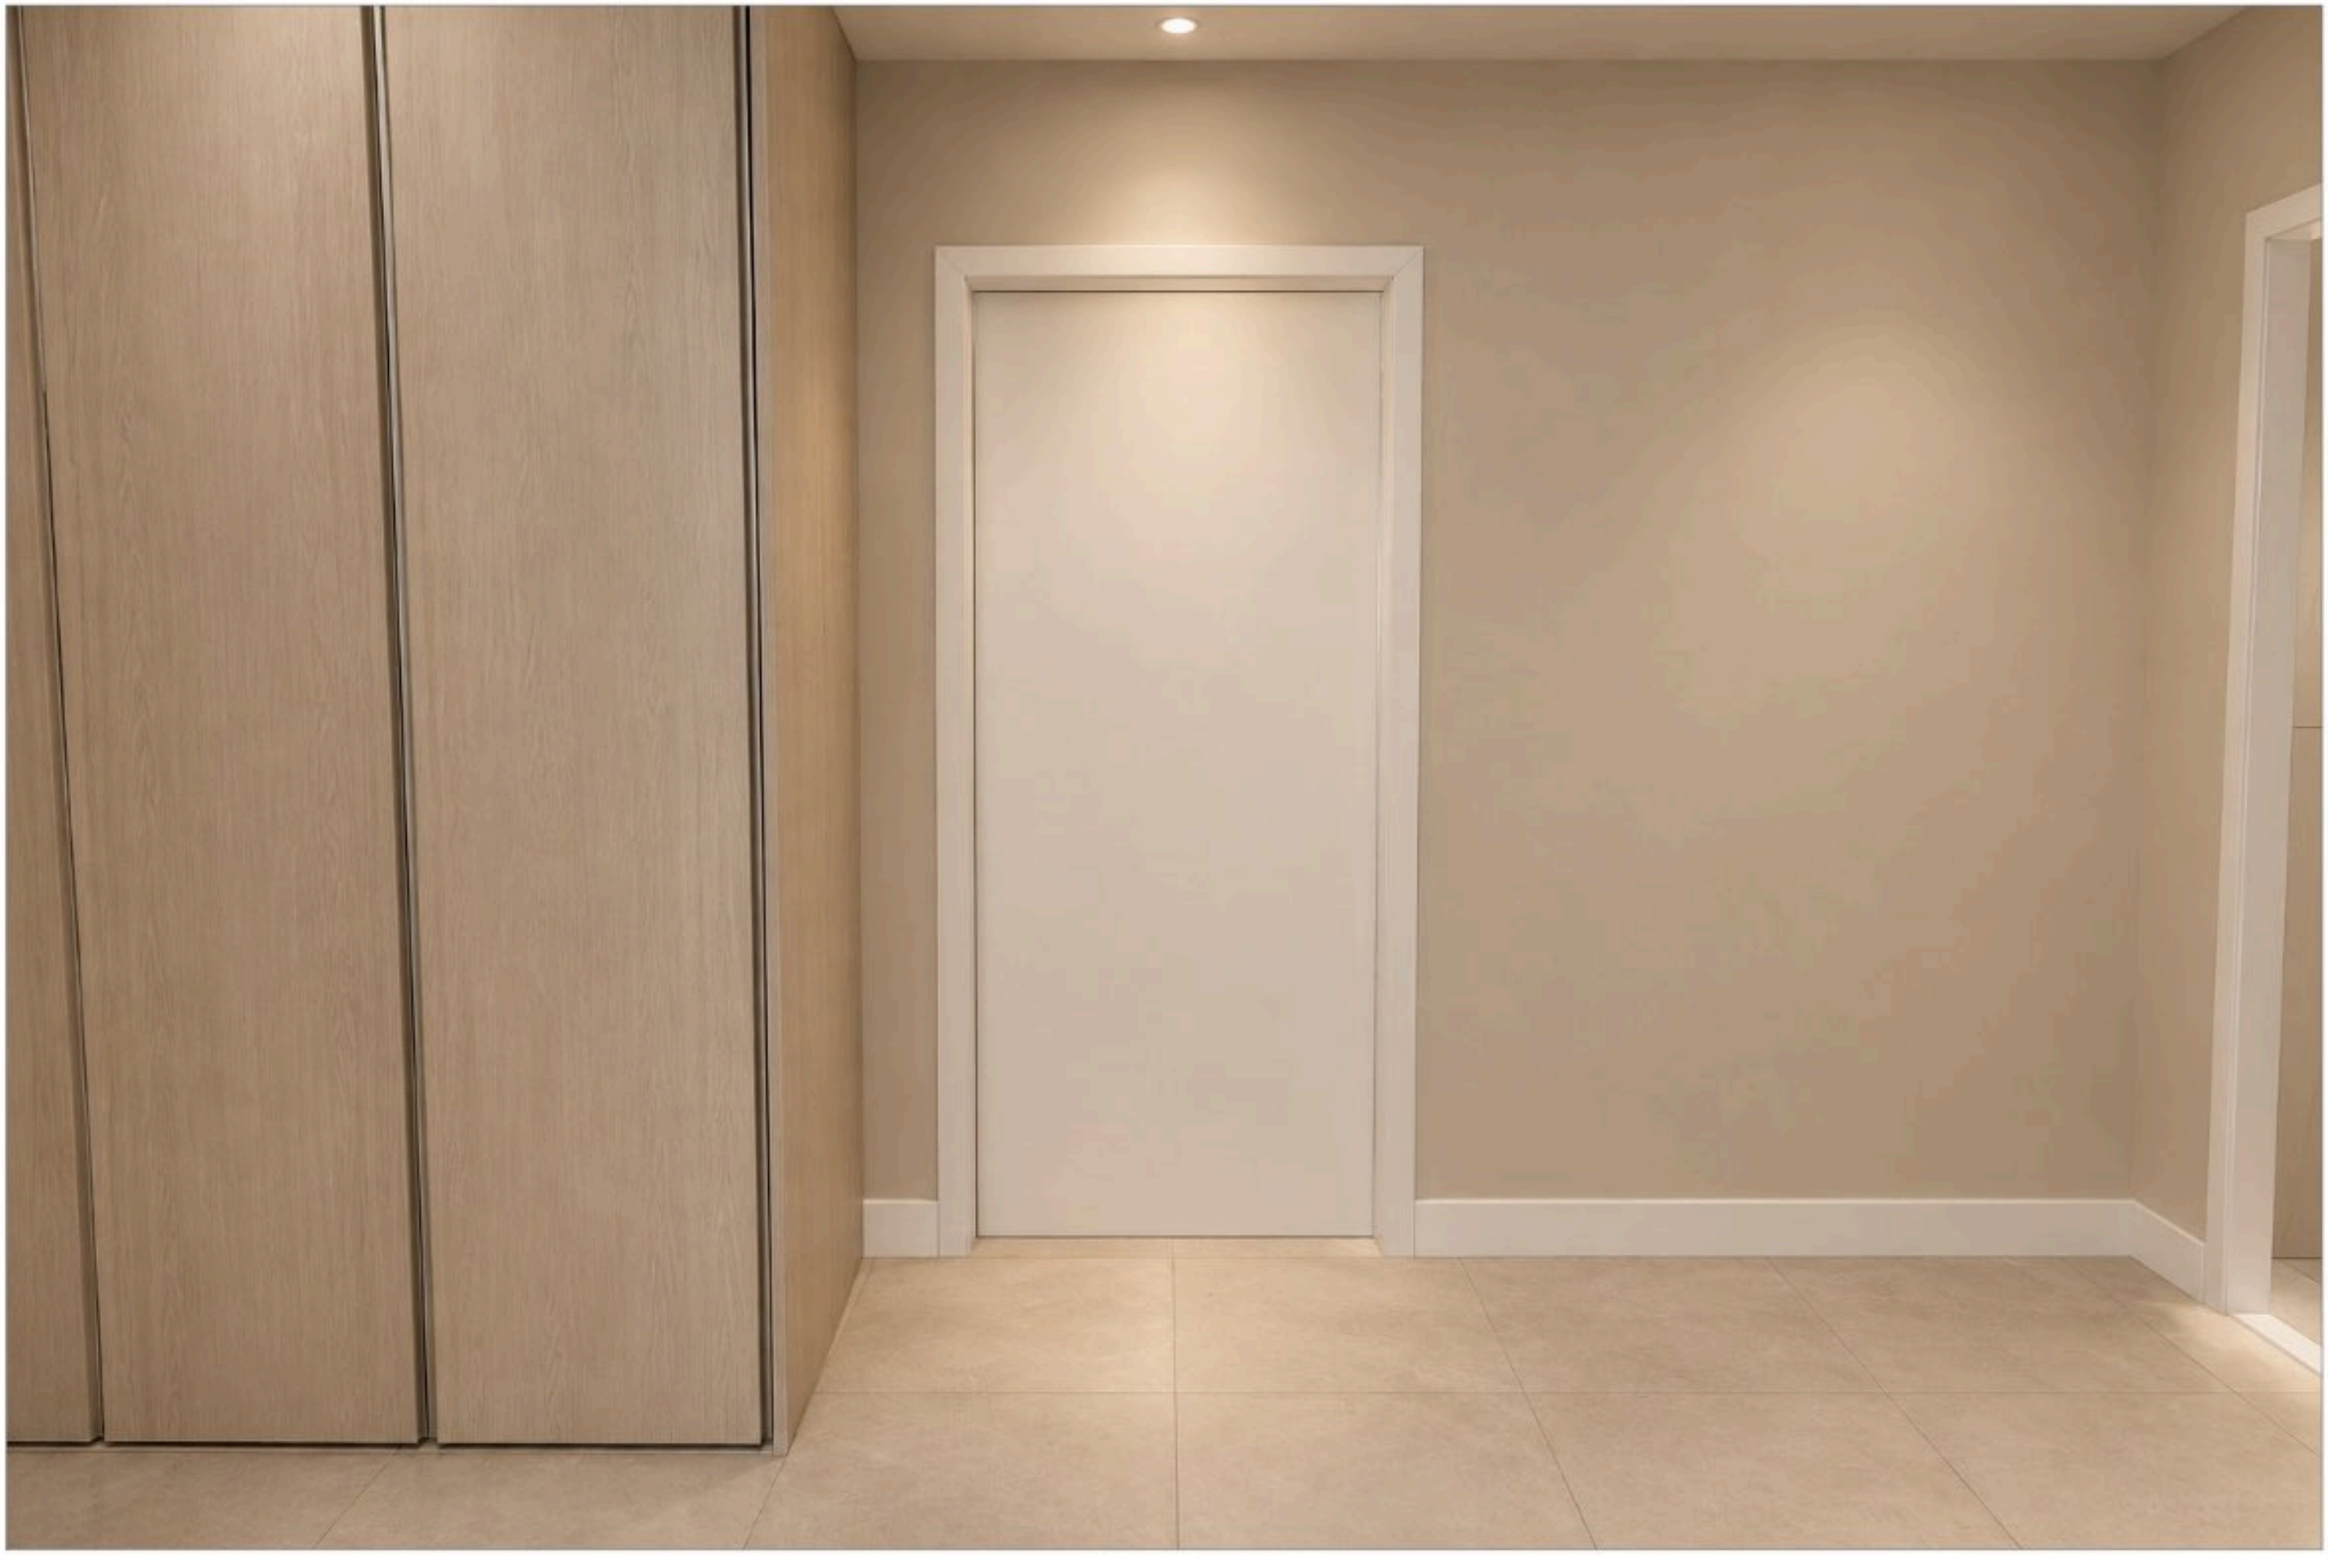


| | | | | | | |
|---|---|---|---|---|---|---|
| | | | | | Проект: Квартира 58 м² | |
| | Лист | № док. | Подпись | Дата | Визуализация прихожей | Стадия / Лист / Листов |
| Дизайнер | Кырпан А.С. | | | 09.10.26 | | П / 47 / 60 |

выпуск 09.10.2026 № 6e771c53bc · стр. 47 из 60

## Развёртка стены А

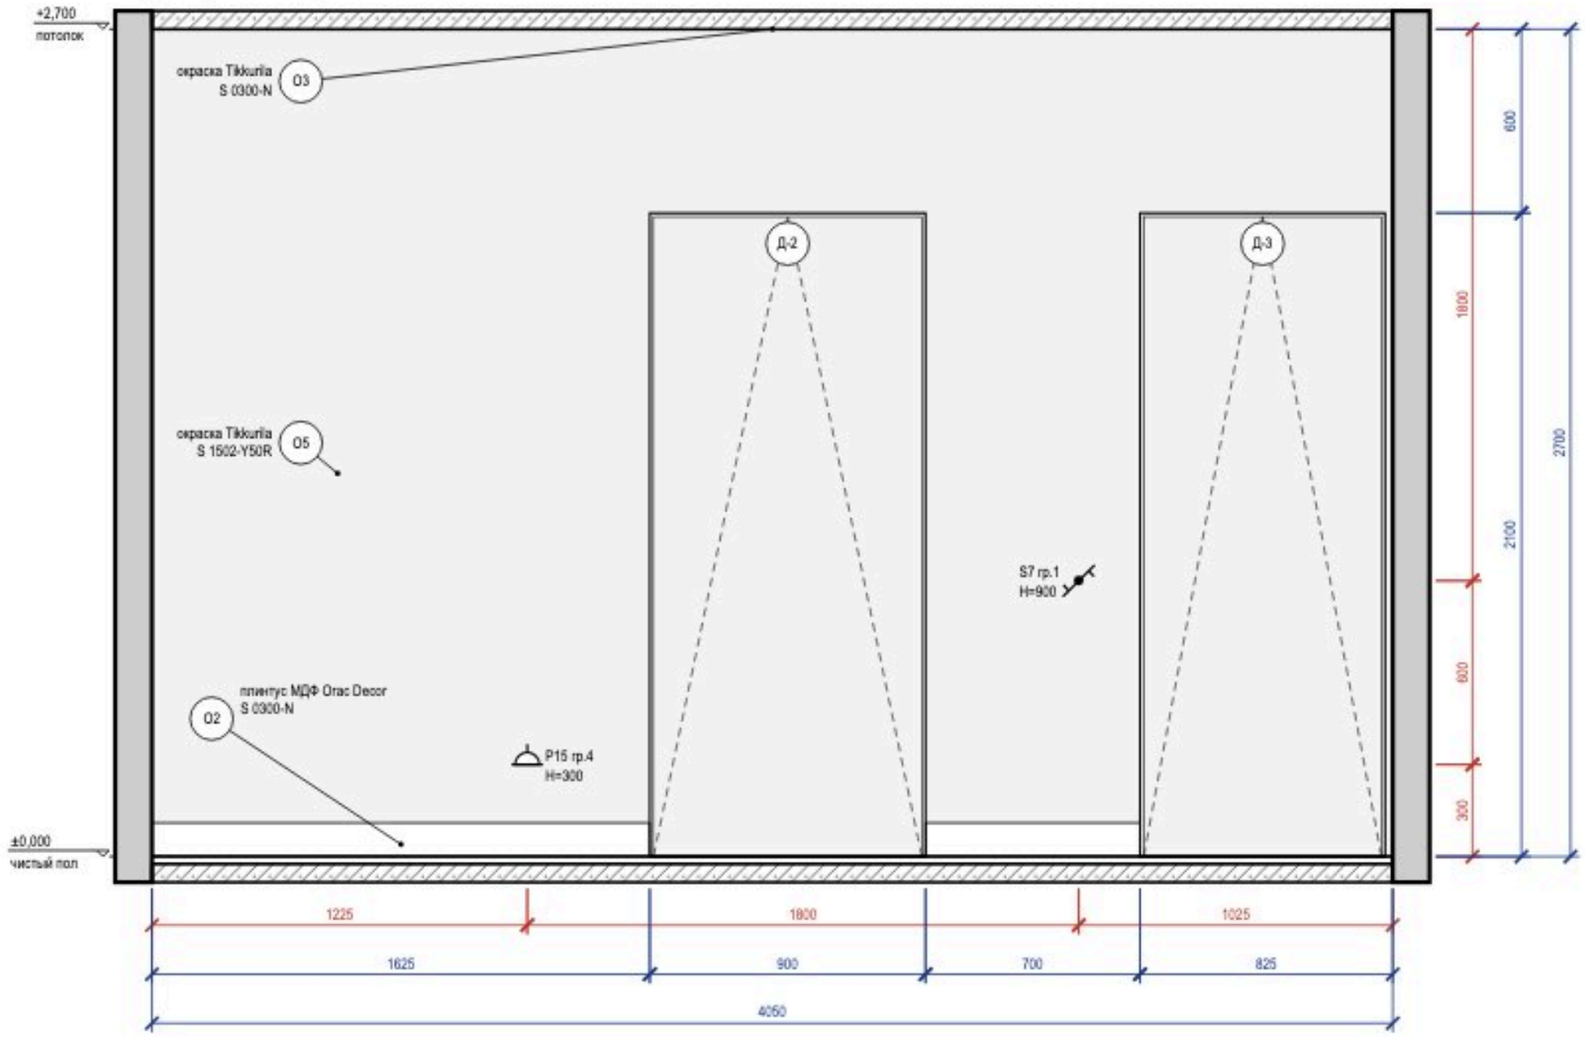



### Схема развёрток (М 1:100)

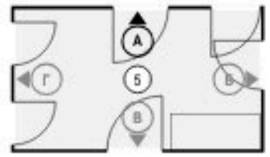


### Ведомость отделки (на листе)

| Марка | Поверхность | Материал, изделие | Цвет, код | Кол. |
|---|---|---|---|---|
| О2 | плинтус | плинтус МДФ, Orac Decor Luxxus, h 110 мм, SX184, шелковисто-матовая | NCS S 0300-N | 2,3 м |
| О3 | потолок | окраска, Tikkurila, глубокоматовая | NCS S 0300-N | 9,6 м² |
| О5 | стены | окраска, Tikkurila, шелковисто-матовая, подготовка О3 | NCS S 1502-Y50R | 7,4 м² |

Визуализация этой стены — лист 46

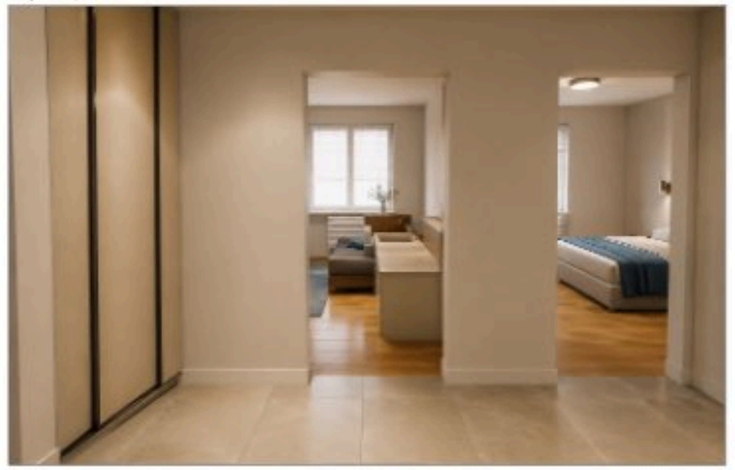


### Примечания

1. Размеры — в мм от чистовых поверхностей стен; условные обозначения и общие указания — лист 2.
2. Двери скрытого монтажа — полотно в плоскости стены, отделка стены по полотну, плинтус прерывается у короба (узел — на листе узлов).


| | | | | | Проект: Квартира 58 м² | | | |
|---|---|---|---|---|---|---|---|---|
| | Лист | № док. | Подпись | Дата | Развёртка стены А. Прихожая (пом. 5) | Стадия | Лист | Листов |
| Дизайнер | Кырпан А.С. | | | 09.10.26 | | П | 48 | 60 |

выпуск 09.10.2026 · 6e771c53bc · стр. 48 из 60

## Развёртка стены Б

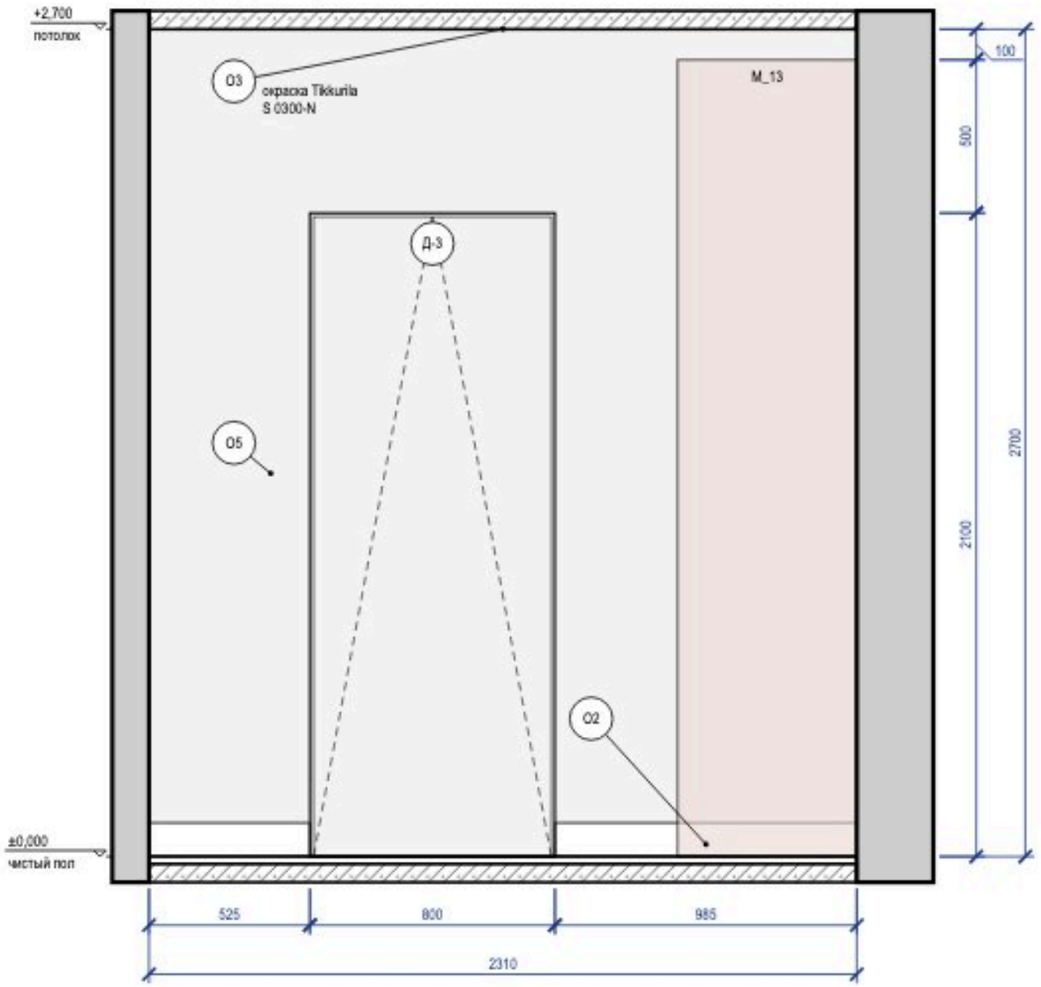


### Схема развёрток (М 1:100)

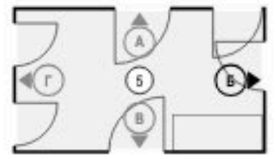


### Ведомость отделки (на листе)

| Марка | Поверхность | Материал, изделие | Цвет, код | Кол. |
|---|---|---|---|---|
| О2 | плинтус | плинтус МДФ, Orac Decor Luxxus, h 110 мм, SX184, шелковисто-матовая | NCS S 0300-N | 1,5 м |
| О3 | потолок | окраска, Tikkurila, глубокоматовая | NCS S 0300-N | 9,6 м² |
| О5 | стены | окраска, Tikkurila, шелковисто-матовая, подготовка О3 | NCS S 1502-Y50R | 4,6 м² |


### Примечания

1. Размеры — в мм от чистовых поверхностей стен; условные обозначения и общие указания — лист 2.
2. Двери скрытого монтажа — полотно в плоскости стены, отделка стены по полотну, плинтус прерывается у короба (узел — на листе узлов).

| | | | | | | |
|---|---|---|---|---|---|---|
| | | | | | Проект: Квартира 58 м² | |
| | Лист | № док. | Подпись | Дата | Развёртка стены Б. Прихожая (пом. 5) | Стадия / Лист / Листов |
| Дизайнер | Кырпан А.С. | | | 09.10.26 | | П / 49 / 60 |

выпуск 09.10.2026 № 6e771c53bc · стр. 49 из 60

## Развёртка стены В

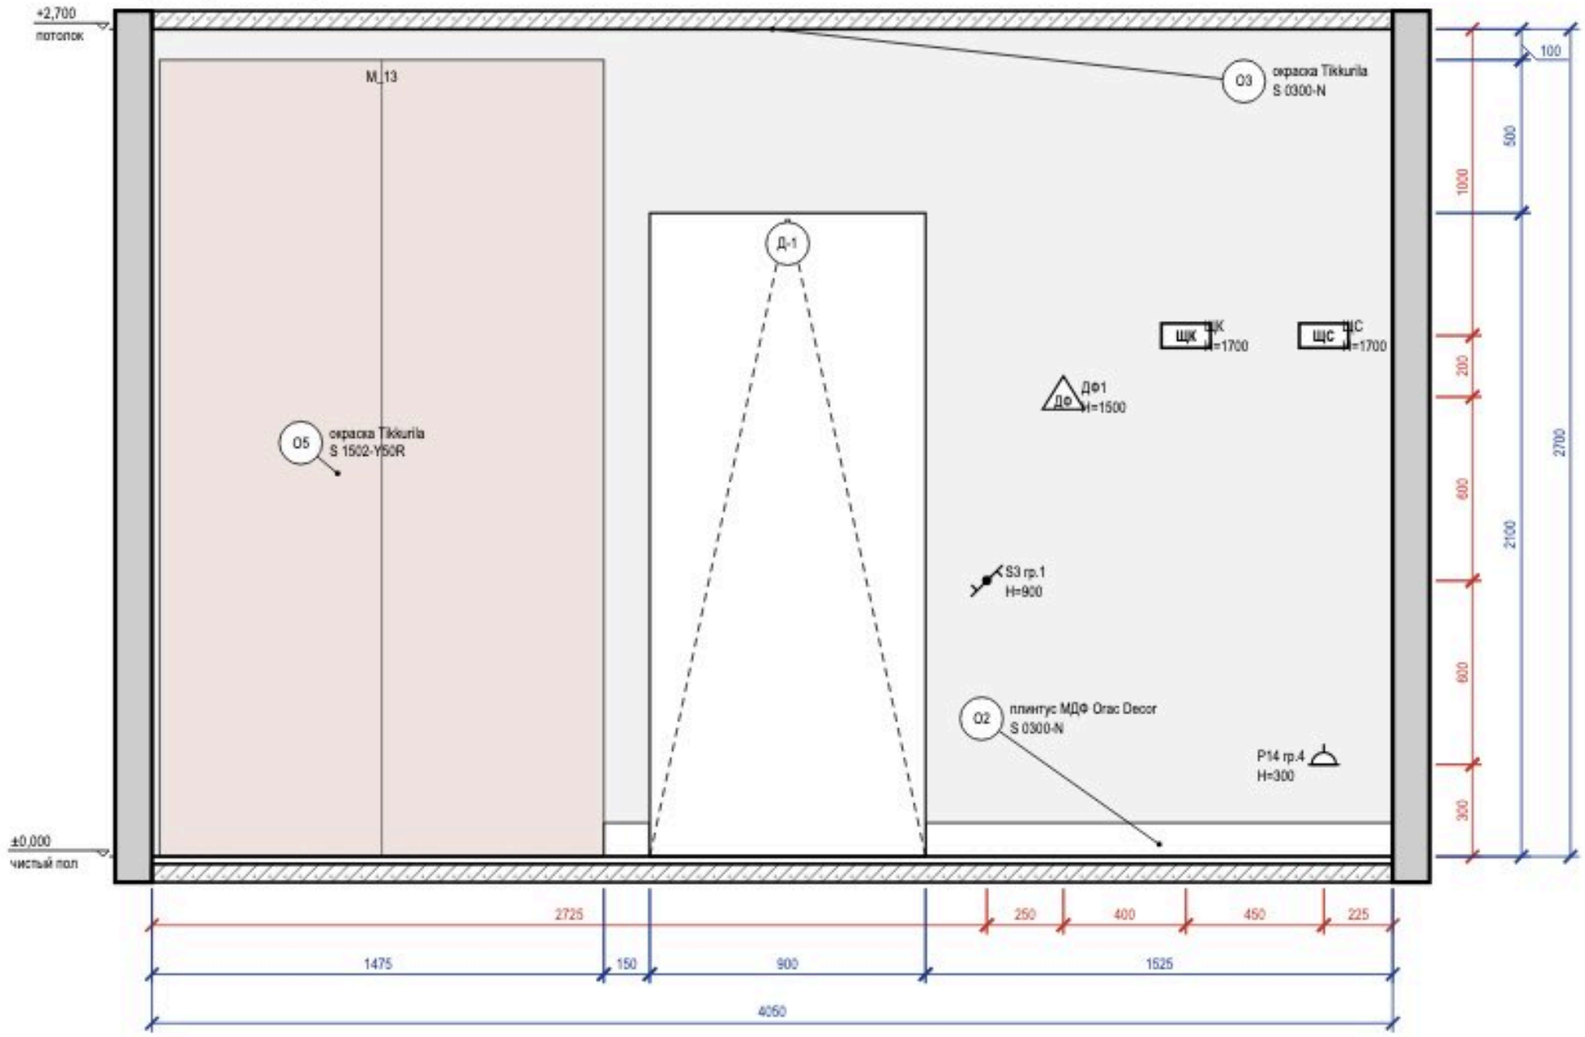



### Схема развёрток (М 1:100)




### Ведомость отделки (на листе)

| Марка | Поверхность | Материал, изделие | Цвет, код | Кол. |
|---|---|---|---|---|
| О2 | плинтус | плинтус МДФ, Orac Decor Luxxus, h 110 мм, SX184, шелковисто-матовая | NCS S 0300-N | 1,7 м |
| О3 | потолок | окраска, Tikkurila, глубокоматовая | NCS S 0300-N | 9,6 м² |
| О5 | стены | окраска, Tikkurila, шелковисто-матовая, подготовка О3 | NCS S 1502-Y50R | 9 м² |

Визуализация этой стены — лист 47

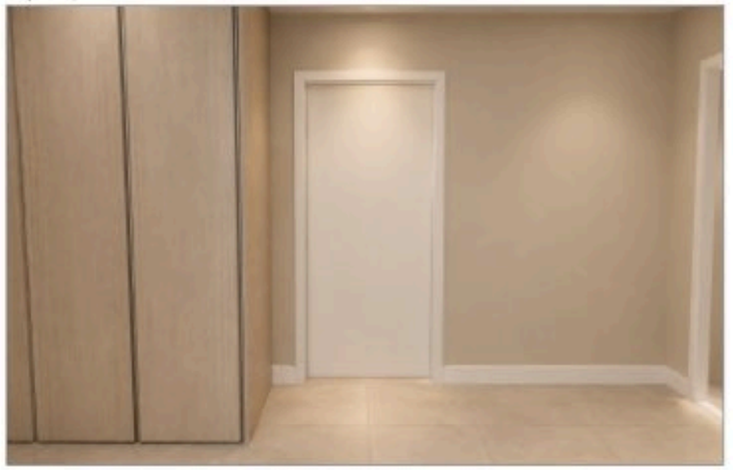

### Примечания


1. Размеры — в мм от чистовых поверхностей стен; условные обозначения и общие указания — лист 2.

| | | | | | |
|---|---|---|---|---|---|
| | Лист | № док. | Подпись | Дата | Проект: Квартира 58 м² |
| Дизайнер | Кырпан А.С. | | | 09.10.26 | Развёртка стены В. Прихожая (пом. 5) |


| Стадия | Лист | Листов |
|---|---|---|
| П | 50 | 60 |

выпуск 09.10.2026 № 6e771c53bc · стр. 50 из 60

## Развёртка стены Г

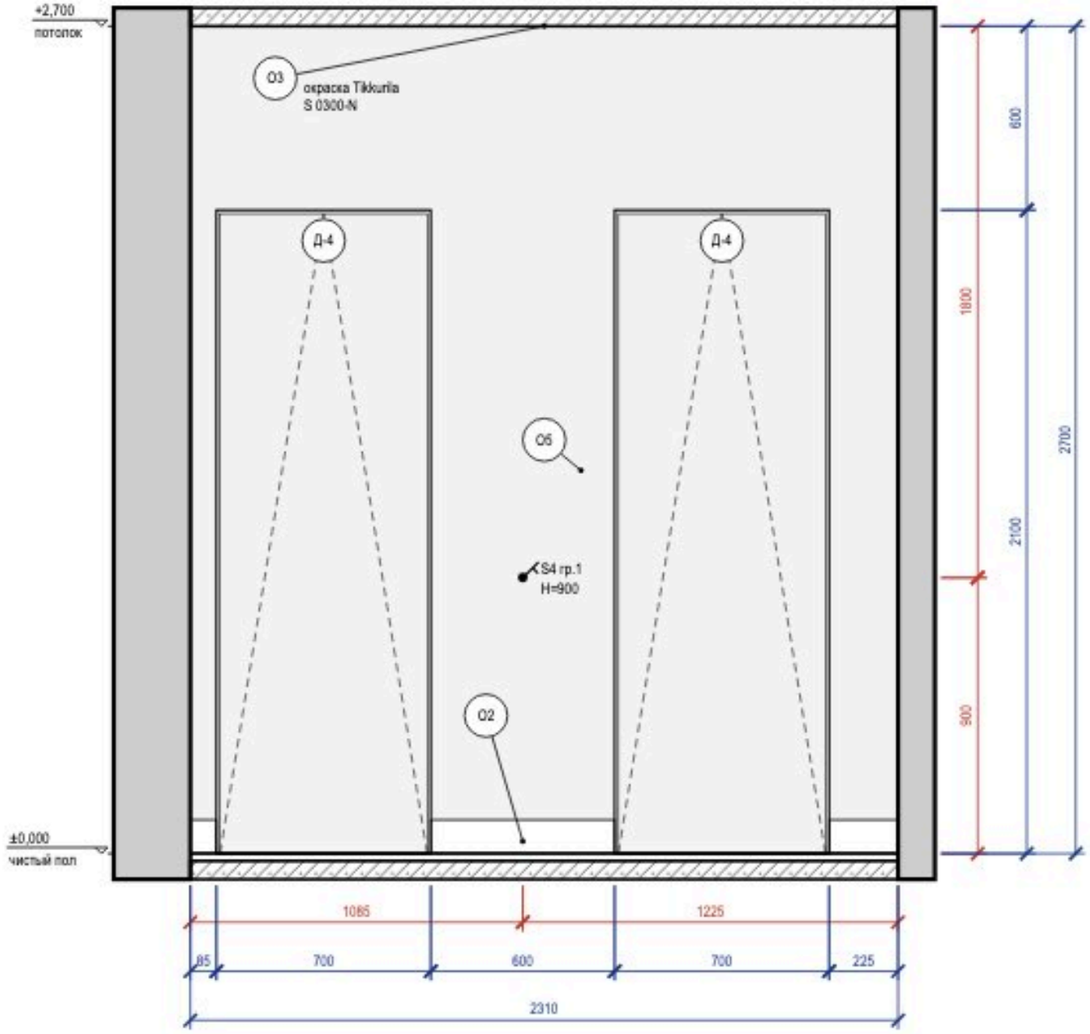


### Схема разверток (М 1:100)

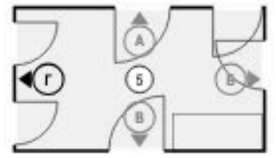


### Ведомость отделки (на листе)

| Марка | Поверхность | Материал, изделие | Цвет, код | Кол. |
|---|---|---|---|---|
| О2 | плинтус | плинтус МДФ, Orac Decor Luxxus, h 110 мм, SX184, шелковисто-матовая | NCS S 0300-N | 0,9 м |
| О3 | потолок | окраска, Tikkurila, глубокоматовая | NCS S 0300-N | 9,6 м² |
| О5 | стены | окраска, Tikkurila, шелковисто-матовая, подготовка Q3 | NCS S 1502-Y50R | 3,3 м² |

### Примечания

1. Размеры — в мм от чистовых поверхностей стен; условные обозначения и общие указания — лист 2.
2. Двери скрытого монтажа — полотно в плоскости стены, отделка стены по полотну, плинтус прерывается у короба (узел — на листе узлов).

| | | | | | |
|---|---|---|---|---|---|
| | | | | | Проект: Квартира 58 м² |
| | Лист | № док. | Подпись | Дата | Развёртка стены Г. Прихожая (пом. 5) |
| Дизайнер | Кырпан А.С. | | | 09.10.26 | |

| Стадия | Лист | Листов |
|---|---|---|
| П | 51 | 60 |


выпуск 09.10.2026 № 6e771c53bc · стр. 51 из 60




| | | | | | | |
|---|---|---|---|---|---|---|
| | | | | | Проект: Квартира 58 м² | |
| | Лист | № док. | Подпись | Дата | Визуализация гардеробной | Стадия / Лист / Листов |
| Дизайнер | Кырпан А.С. | | | 09.10.26 | | П / 52 / 60 |

выпуск 09.10.2026 № 6e771c53bc · стр. 52 из 60


## Развёртка стены А

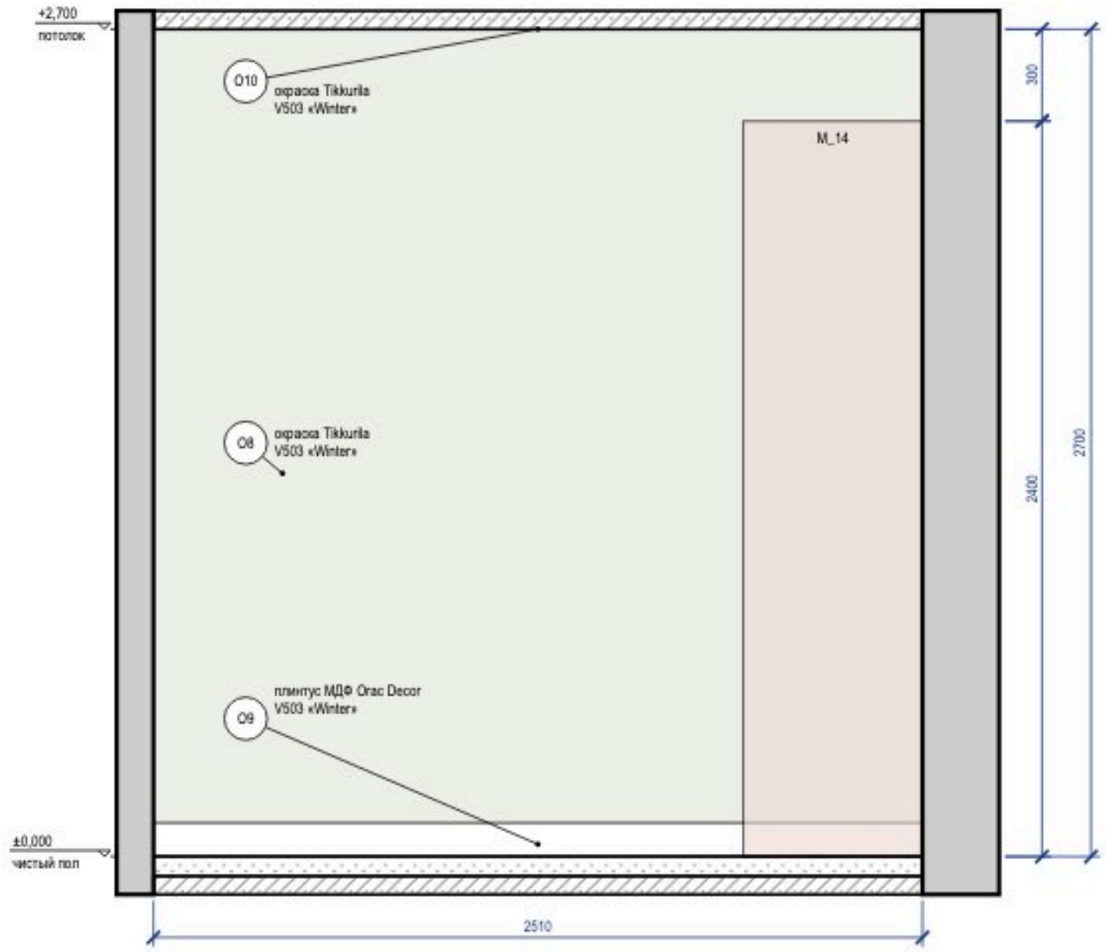


## Развёртка стены Б

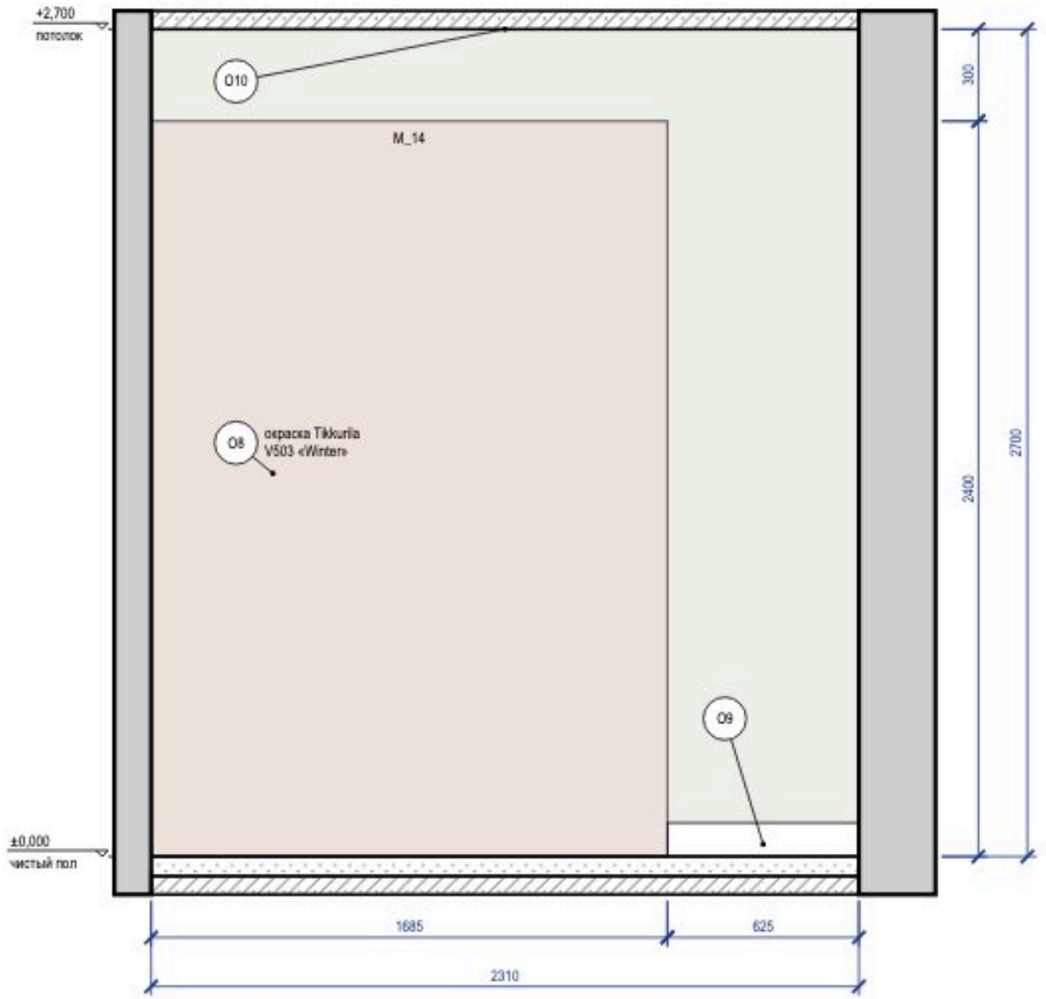



### Схема развёрток (М 1:100)

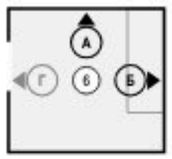


### Ведомость отделки (на листе)

| Марка | Поверхность | Материал, изделие | Цвет, код | Кол. |
|---|---|---|---|---|
| О8 | стены | окраска, Tikkurila Harmony, матовая, подготовка Q3 | Tikkurila V503 «Winter» | 13 м² |
| О9 | плинтус | плинтус МДФ, Orac Decor Luxeus, h 110 мм, SX184 | Tikkurila V503 «Winter» | 3,1 м |
| О10 | потолок | окраска, Tikkurila Anti-Reflex 2, глубокоматовая, подготовка Q3 | Tikkurila V503 «Winter» | 5,9 м² |

Визуализация этой стены — лист 52

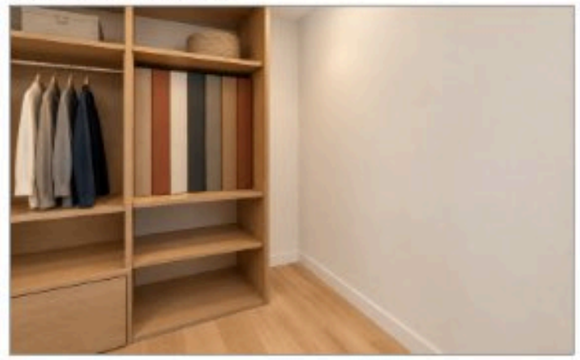

### Примечания


1. Размеры — в мм от чистовых поверхностей стен; условные обозначения и общие указания — лист 2.

| | | | | | |
|---|---|---|---|---|---|
| | Лист | № док. | Подпись | Дата | Проект: Квартира 58 м² |
| Дизайнер | Кырпан А.С. | | | 09.10.26 | Развёртки стен А, Б. Гардеробная (пом. 6) |


| Стадия | Лист | Листов |
|---|---|---|
| П | 53 | 60 |

выпуск 09.10.2026 № 6e771c53bc · стр. 53 из 60

## Развёртка стены Г

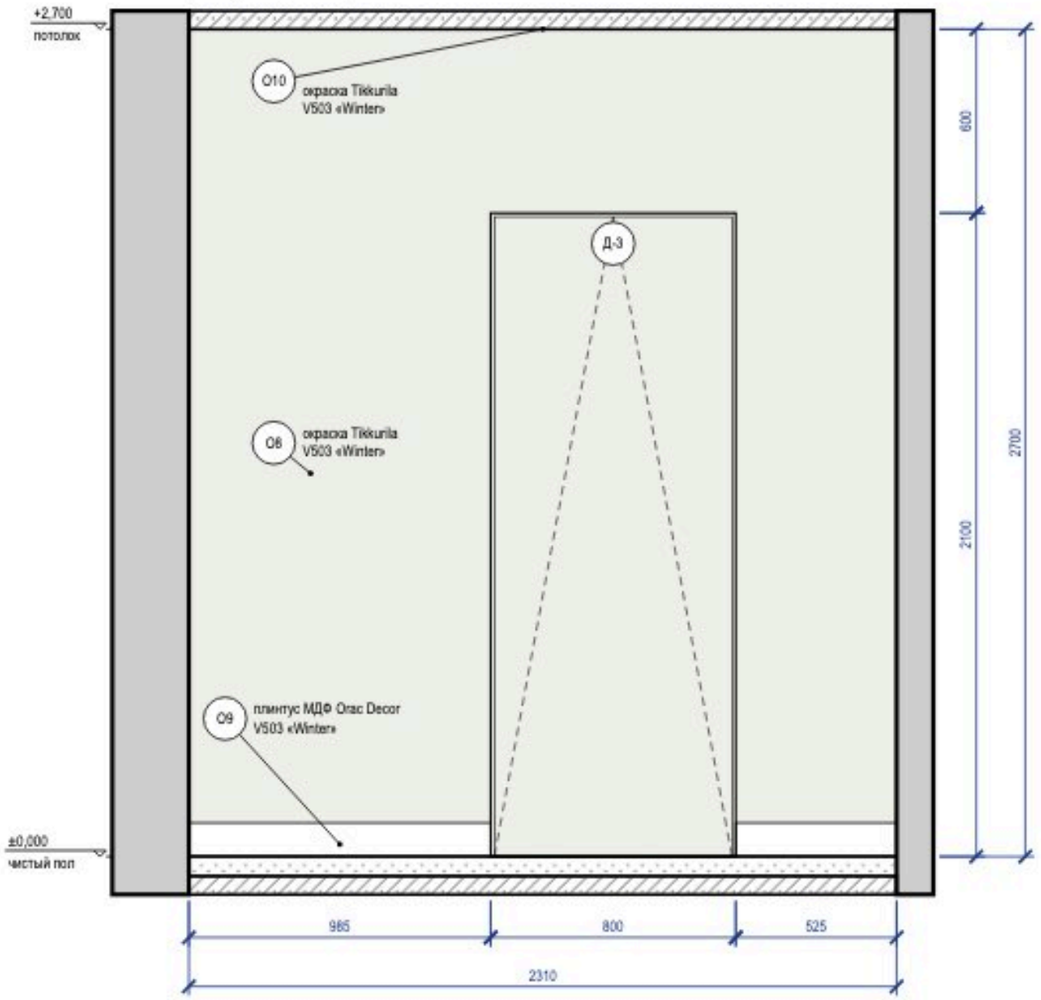


## Схема развёрток (М 1:100)

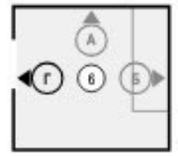


## Ведомость отделки (на листе)

| Марка | Поверхность | Материал, изделие | Цвет, код | Кол. |
|---|---|---|---|---|
| О8 | стены | окраска, Tikkurila Harmony, матовая, подготовка Q3 | Tikkurila V503 «Winter» | 4,6 м² |
| О9 | плинтус | плинтус МДФ, Orac Decor Luxxus, h 110 мм, SX184 | Tikkurila V503 «Winter» | 1,5 м |
| О10 | потолок | окраска, Tikkurila Anti-Reflex 2, глубокоматовая, подготовка Q3 | Tikkurila V503 «Winter» | 5,9 м² |

## Примечания


1. Размеры — в мм от чистовых поверхностей стен; условные обозначения и общие указания — лист 2.
2. Двери скрытого монтажа — полотно в плоскости стены, отделка стены по полотну, плинтус прерывается у короба (узел — на листе узлов).

| | | | | | |
|---|---|---|---|---|---|
| | | | | | Проект: Квартира 58 м² |
| | Лист | № док. | Подпись | Дата | Развёртка стены Г. Гардеробная (пом. 6) |
| Дизайнер | Кырпан А.С. | | | 09.10.26 | |


| Стадия | Лист | Листов |
|---|---|---|
| П | 54 | 60 |

выпуск 09.10.2026 № 6e771c53bc · стр. 54 из 60


**Вид с фасадами**

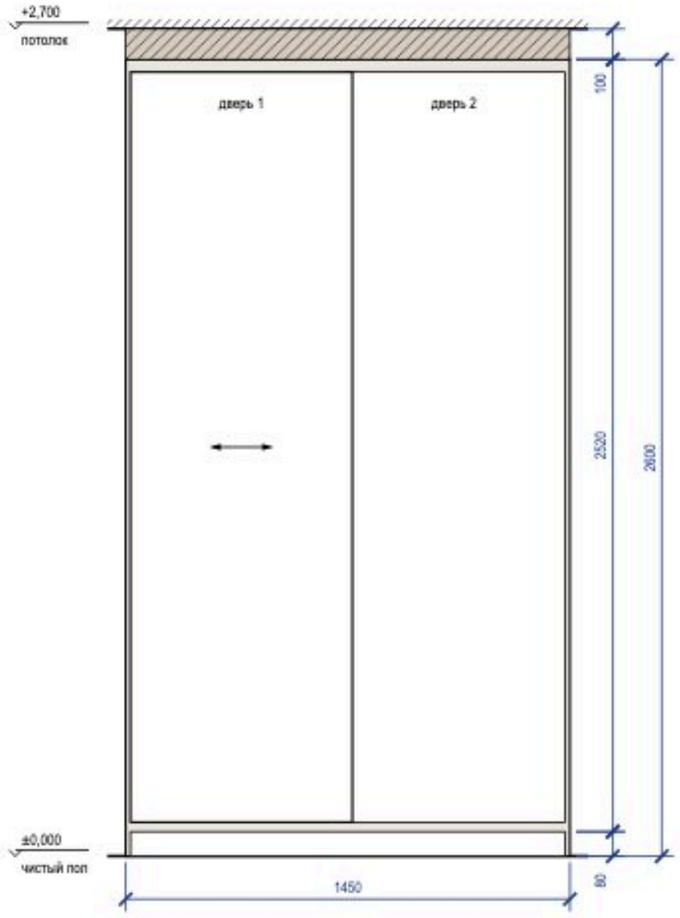



**Вид без фасадов**

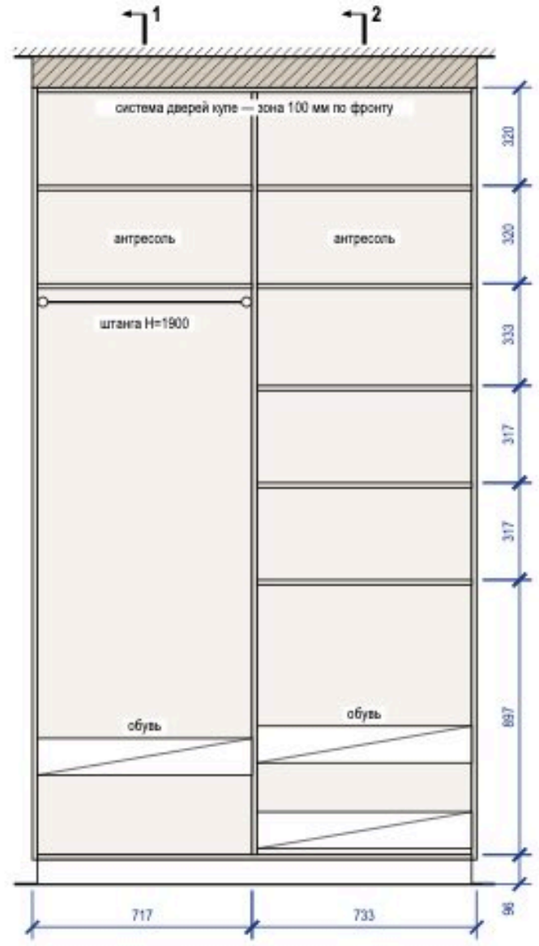


**Разрез 1-1**

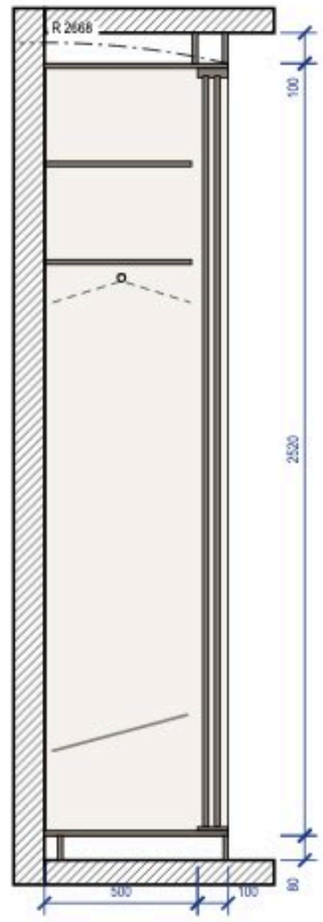



**Разрез 2-2**

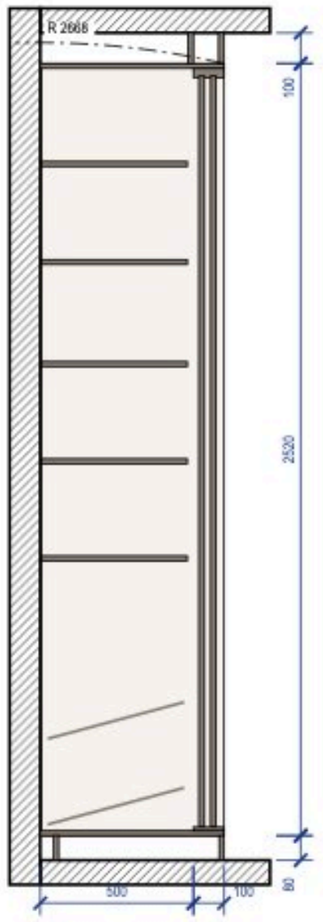


## Примечания

1. Размеры — в мм по чистовой отделке; изделие 1450×600×2600 (Ш×Г×В). Перед раскроем — контрольный замер цеха после чистовой отделки стен, пола и потолка.
2. Корпус — ЛДСП 16 мм, задняя стенка ХДФ 4 мм в паз, цоколь 80 мм на регулируемых опорах; двери купе — ЛДСП 10 мм в алюминиевом профиле, наклёст 30 мм, ширина двери 724 мм, высота — проём минус 40 мм; цвет — по колерной карте.
3. Кромка: скрытые торцы 0,4 мм, видимые 1 мм (ПВХ/АБС).
4. Номинальные зазоры: дверь купе — боковина 3 мм, фасад ящика — стойка 2 мм; ящики внутри купе — с накладкой 30 мм на стойке со стороны наклёста дверей.
5. Ящики — направляющие полного выдвижения NL 450 (внутренняя глубина 496 мм ≥ NL + 3); присадка по 32-й системе — выполняет цех.
6. Компенсатор 100 мм — короб из ЛДСП по фронту и торцам, подгоняется к потолку при монтаже (припуск 20 мм), крепится к корпусу и к потолку.
7. Подъём корпуса: диагональ боковины $\sqrt{(2600^2 + 600^2)} = 2668$ мм < 2700 мм до потолка — корпус собирается лёжа и поднимается поворотом.
8. Крепление к стене от опрокидывания — уголки 2 шт. к несущему основанию (монтажная схема шкафов).


**3D орто**

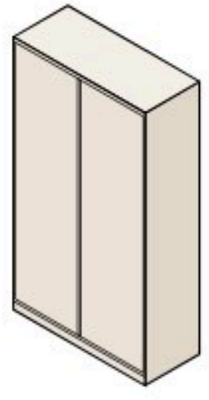


| | | | | | | |
|---|---|---|---|---|---|---|
| | | | | | Проект: Квартира 58 м² | |
| | Лист | № док. | Подпись | Дата | Шкаф-купе M_13 | Стадия / Лист / Листов |
| Дизайнер | Кырпан А.С. | | | 09.10.26 | | П / Д_1 / 60 |

выпуск 09.10.2026 · 6e771c53bc · стр. 55 из 60


## Общий вид

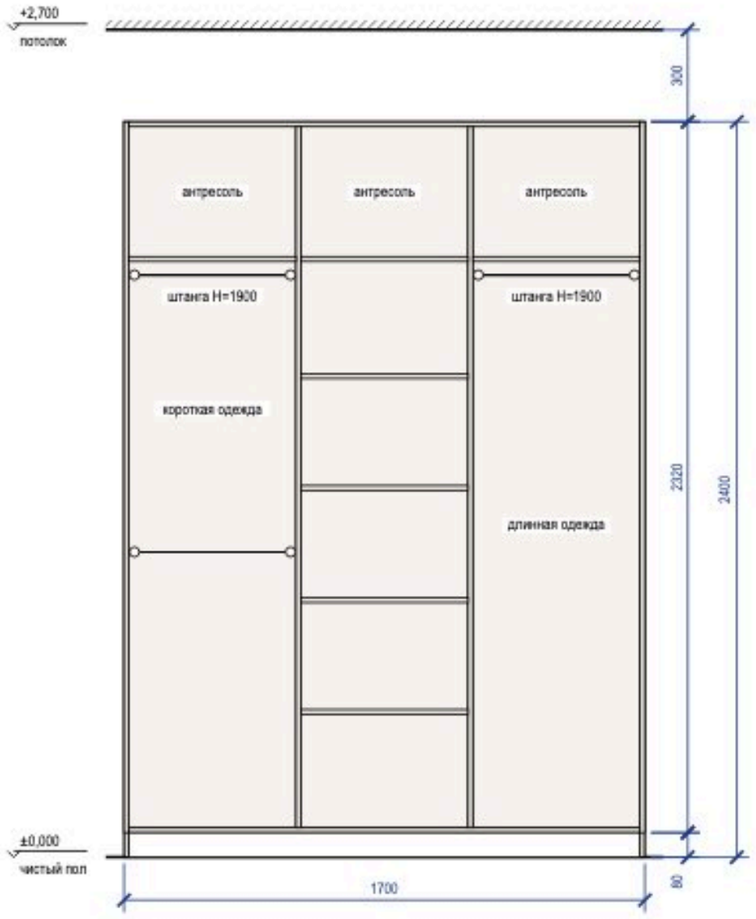



## Наполнение, размеры в свету

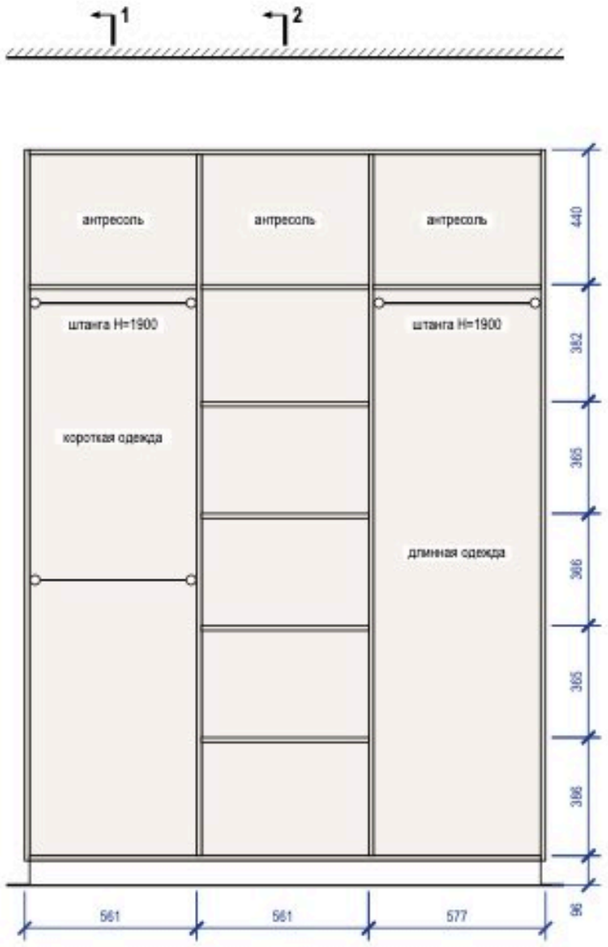


## Разрез 1-1

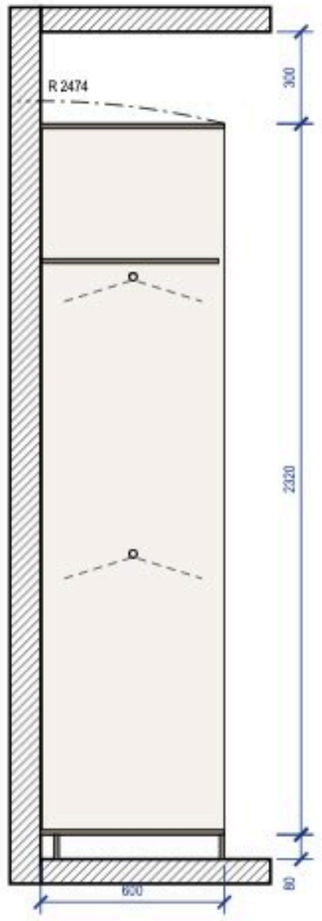



## Разрез 2-2

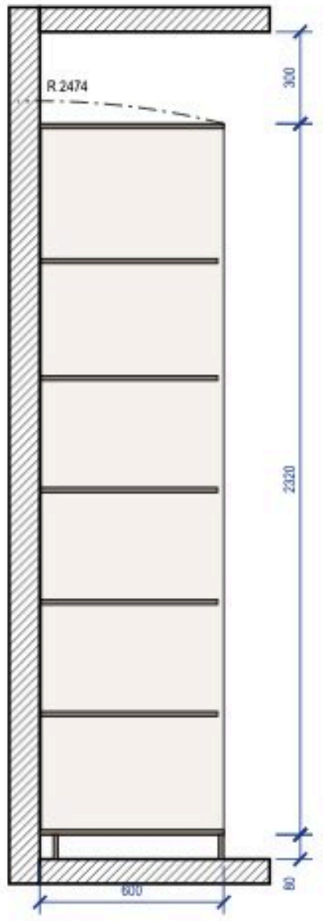


### Примечания

1. Размеры — в мм по чистовой отделке; изделие 1700×600×2400 (Ш×Г×В). Перед раскроем — контрольный замер цеха после чистовой отделки стен, пола и потолка.
2. Корпус — ЛДСП 16 мм, задняя стенка ХДФ 4 мм в паз, цоколь 80 мм на регулируемых опорах; открытая система без фасадов, ящики с фасадами.
3. Кромка: скрытые торцы 0,4 мм, видимые 2 мм (ПВХ/АБС).
4. Номинальные зазоры: между фасадами ящиков 3 мм, фасад ящика — стойка 2 мм.
5. Ящики — направляющие полного выдвижения NL 550 (внутренняя глубина 596 мм ≥ NL + 3); присадка по 32-й системе — выполняет цех.
6. Зазор до потолка 300 мм.
7. Подъём корпуса: диагональ боковины $\sqrt{(2400^2 + 600^2)} = 2474$ мм < 2700 мм до потолка — корпус собирается лёжа и поднимается поворотом.
8. Крепление к стене от опрокидывания: крепление к стене, 3 точки; основание стены и шаг анкеров — монтажная схема шкафов.


## 3D орто

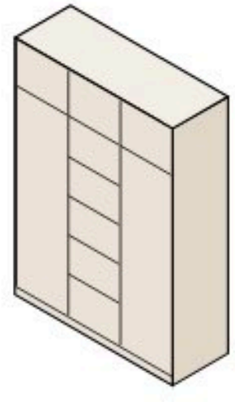


| | | | | | | |
|---|---|---|---|---|---|---|
| | | | | | Проект: Квартира 58 м² | |
| | Лист | № док. | Подпись | Дата | Система хранения M_14 | Стадия / Лист / Листов |
| Дизайнер | Кырпан А.С. | | | 09.10.26 | | П / Д_2 / 60 |

выпуск 09.10.2026 № 6e771c53bc · стр. 56 из 60


## Вид с фасадами

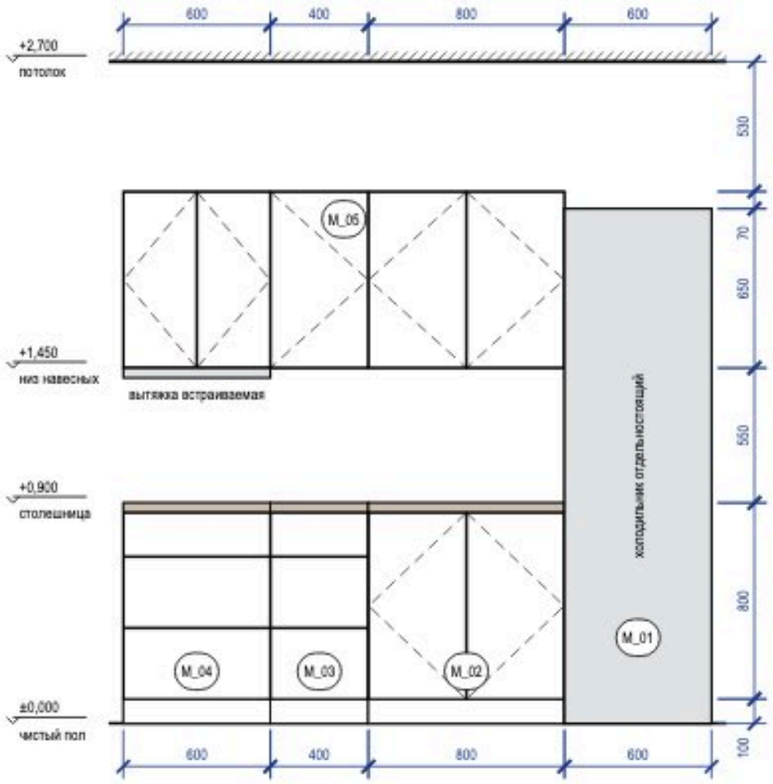



## Вид без фасадов (наполнение, выводы)

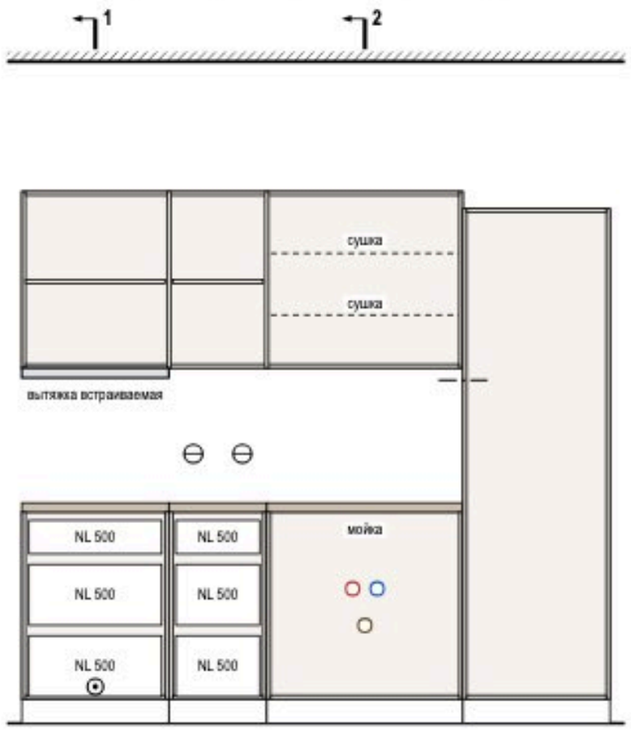



## Разрез 1-1

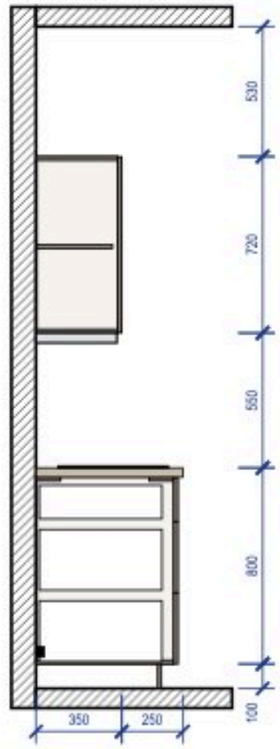


## Разрез 2-2

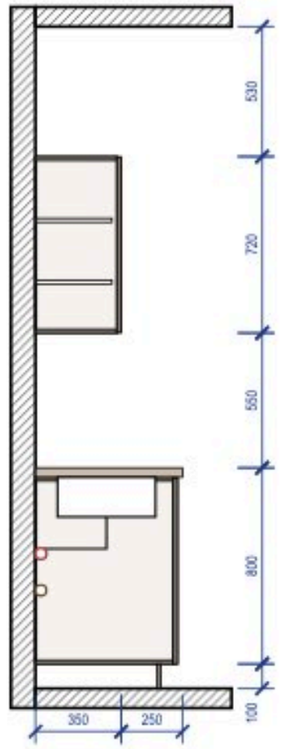


## 3D орто

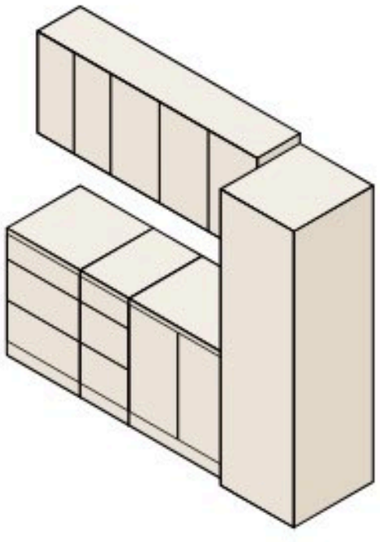

## Примечания

1. Размеры — в мм по чистовой отделке, вид из помещения; марки — как на плане расстановки. Перед раскроем — контрольный замер цеха после фартука и пола.
2. Корпуса — ЛДСП 16 мм, задняя стенка ХДФ 4 мм; фасады — МДФ эмаль 18 мм, цвет по колерной карте; столешница 38 мм, свес 20 мм; цоколь 100 мм.
3. Кромка: скрытые торцы 0,4 мм, видимые 1 мм. Номинальные зазоры: между фасадами 3 мм, фасад — столешница 3 мм, фасад — стена не менее 3 мм.
4. Ящики полного выдвижения и петли — с доводчиком; присадка по 32-й системе — выполняет цех.
5. Вытяжка встраивается в навесной модуль над варочной: её низ 510 мм над панелью — меньше 650 мм, модуль поднять или принять вытяжку с допуском по паспорту модели.
6. Ниши техники — по монтажным схемам выбранных моделей: решётка в цоколе и канал за пеналом холодильника, зазор за духовым шкафом, фасад ПММ на двери машины.

| | | | | | | |
|---|---|---|---|---|---|---|
| | | | | | Проект: Квартира 58 м² | |
| | Лист | № док. | Подпись | Дата | Кухня (пом. 1). Развёртка гарнитура | Стадия / Лист / Листов |
| Дизайнер | Кырпан А.С. | | | 09.10.26 | | П / Д_3 / 60 |

выпуск 09.10.2026 · 6e771c53bc · стр. 57 из 60

## Ведомость отделки помещений (форма 1 прил. А ГОСТ 21.501-2018)

| № | Наименование помещения | Потолок | | | Стены и перегородки | | | Низ стен (плинтус) | | | Пол | | Примечание |
|---|---|---|---|---|---|---|---|---|---|---|---|---|---|
| | | Вид отделки | Код цвета | S, м² | Вид отделки | Код цвета | S, м² | Вид отделки | Код цвета | L, м | Вид отделки | S, м² | |
| 1 | Кухня-гостиная 21,04 м² | Окраска, Tikkurila, глубокоматовая | NCS S 0300-N | 21,04 | Окраска, Tikkurila, полуматовая, подготовка Q3 | NCS S 1002-Y50R | 43,10 | Плинтус МДФ h=110 мм, SX184 | NCS S 0300-N | 17,7 | Инженерная доска, IM1861, 1380×190 мм, на клею; тип 1, отм. ЧП ±0,000 | 21,04 | Н стен 2700 (до потолка) |
| 2 | Спальня 13,95 м² | Окраска, Tikkurila, глубокоматовая | NCS S 0300-N | 13,95 | Окраска, Tikkurila, глубокоматовая, подготовка Q3 | NCS S 1502-Y50R | 36,15 | Плинтус МДФ h=110 мм, SX184 | NCS S 0300-N | 14,2 | Инженерная доска, IM1861, 1380×190 мм, на клею; тип 1, отм. ЧП ±0,000 | 13,95 | Н стен 2700 (до потолка) |
| 3 | Ванная 2,95 м² | Окраска, Tikkurila, глубокоматовая | NCS S 0300-N | 2,95 | Облицовка плиткой, 610015000370, 600×1200 мм, клей С2 | Italon 610015000370 | 17,64 | нет (облицовка от пола) | | | Керамогранит, SG651622R, 600×600 мм; тип 2, отм. ЧП −0,015 | 2,96 | Н стен 2715 (до потолка); тёплый пол; гидроизоляция обмазочная, 2 слоя, с заведением на стены 200 мм (по периметру пола); тест проливом и акт скрытых работ |
| 4 | Санузел 1,80 м² | Окраска, Tikkurila, глубокоматовая | NCS S 0300-N | 1,80 | Облицовка плиткой, 610015000370, 600×1200 мм, клей С2 | Italon 610015000370 | 14,71 | нет (облицовка от пола) | | | Керамогранит, SG651622R, 600×600 мм; тип 2, отм. ЧП −0,015 | 1,80 | Н стен 2715 (до потолка); гидроизоляция обмазочная, 2 слоя, с заведением на стены 200 мм (по периметру пола); тест проливом и акт скрытых работ |
| 5 | Прихожая 9,55 м² | Окраска, Tikkurila, глубокоматовая | NCS S 0300-N | 9,55 | Окраска, Tikkurila, полуматовая, подготовка Q3 | NCS S 1502-Y50R | 24,59 | Плинтус МДФ h=110 мм, SX184 | NCS S 0300-N | 8,0 | Керамогранит, SG651622R, 600×600 мм; тип 3, отм. ЧП ±0,000 | 9,55 | Н стен 2700 (до потолка) |
| 6 | Гардеробная 5,94 м² | Окраска, Tikkurila Anti-Reflex 2, глубокоматовая, 2 слоя, подготовка Q3 | Tikkurila V503 | 5,94 | Окраска, Tikkurila Harmony, матовая, 2 слоя, подготовка Q3 | Tikkurila V503 | 24,67 | Плинтус МДФ h=110 мм, SX184 | Tikkurila V503 | 9,0 | Инженерная доска, IM1861, 1380×190 мм, на клею; тип 4, отм. ЧП ±0,000 | 5,94 | Н стен 2700 (до потолка); плинтус в цвет: стены |
| | **Итого** | | | **55,23** | | | **160,87** | | | **48,8** | | **55,23** | |

### Сводка площадей по материалам отделки

| Поверхность | Материал / код цвета | Серия | Площадь, м² |
|---|---|---|---|
| Потолок | NCS S 0300-N | | 49,29 |
| Потолок | Tikkurila V503 | Anti-Reflex 2 | 5,94 |
| Стены | NCS S 1002-Y50R | | 43,10 |
| Стены | NCS S 1502-Y50R | | 60,74 |
| Стены | облицовка плиткой 600×1200 мм, Italon 610015000370 | 610015000370 | 32,36 |
| Стены | Tikkurila V503 | Harmony | 24,67 |

### Примечания

1. Площади поверхностей — по чистым граням стен до отделки: стены = периметр × высоту от чистого пола помещения до низа потолка минус проёмы (облицовка плиткой — до верха облицовки); плинтус = периметр минус дверные проёмы; пол и потолок — по площади помещения. Количество плиток по раскладке. Площади помещений — с учётом всех частей помещения; откосы в площадь стен не входят.
2. Акцентные стены — отдельными строками, их площадь вычтена из основной отделки стен помещения.
3. Плинтус — длина по периметру за вычетом дверных проёмов; примыкания к наличникам и встроенной мебели — по развёрткам.
4. Формат плитки — Ш×В×Т (ширина × высота в положении укладки × толщина), мм; на полу — вдоль стен А/В × вдоль стен Б/Г.
5. Коды цвета — по веерам производителей; колеровка каждой краски одной партией, проверка выкраса при свете D65 и при лампах проекта.
6. Уровни подготовки Q1–Q4 — система Knauf, не норма ГОСТ/СП; допуски поверхностей — по СП 71.13330.2017 (действующая редакция).
7. «аналог=» — изделие задано характеристиками, марку и артикул согласовать с заказчиком до закупки.

| | | | | | Проект: Квартира 58 м² | | | |
|---|---|---|---|---|---|---|---|---|
| | Лист | № док. | Подпись | Дата | Ведомость отделки помещений | Стадия | Лист | Листов |
| Дизайнер | Кырпан А.С. | | | 09.10.26 | | П | С1 | 60 |

выпуск 09.10.2026 № 6e771c53bc · стр. 58 из 60

| Поз. | Наименование и техническая характеристика | Тип, марка, обозначение документа | Код продукции | Поставщик | Ед. изм. | Кол. | Образец | Примечание |
|---|---|---|---|---|---|---|---|---|
| | **Лакокрасочные материалы** | | | | | | | |
| 1 | Краска интерьерная водно-дисперсионная акриловая для стен, полуматовая, класс мокрого истирания 1 по EN 13300, база A; цвет NCS S 1002-Y50R, колеровка машинная | Tikkurila | | Tikkurila | л | 12,6 | | поз. К1 колерной карты; пом. 1; S = 43,1 м² × 2 сл. × 0,12 л/м² = 10,3 л, +10 % и 0,5 л на подкраску → ≥ 11,9 л; тара 1 × 9 л + 1 × 2,7 л + 1 × 0,9 л |
| 2 | Краска интерьерная водно-дисперсионная для потолков, глубокоматовая, класс мокрого истирания 1 по EN 13300, база A; цвет NCS S 0300-N, колеровка машинная | Tikkurila | | Tikkurila | л | 9,9 | | поз. К2 колерной карты; пом. 1, 3, 4, 5; S = 35,3 м² × 2 сл. × 0,12 л/м² = 8,5 л, +10 % и 0,5 л на подкраску → ≥ 9,8 л; тара 1 × 9 л + 1 × 0,9 л |
| 3 | Краска интерьерная водно-дисперсионная акриловая для стен, глубокоматовая, класс мокрого истирания 2 по EN 13300, база A; цвет NCS S 1502-Y50R, колеровка машинная | Tikkurila | | Tikkurila | л | 10,8 | | поз. К4 колерной карты; пом. 2; S = 36,2 м² × 2 сл. × 0,12 л/м² = 8,7 л, +10 % и 0,5 л на подкраску → ≥ 10,0 л; тара 1 × 9 л + 2 × 0,9 л |
| 4 | Краска интерьерная водно-дисперсионная для потолков, глубокоматовая, класс мокрого истирания 2 по EN 13300, база A; цвет NCS S 0300-N, колеровка машинная | Tikkurila | | Tikkurila | л | 4,5 | | поз. К5 колерной карты; пом. 2; S = 13,9 м² × 2 сл. × 0,12 л/м² = 3,3 л, +10 % и 0,5 л на подкраску → ≥ 4,2 л; тара 1 × 2,7 л + 2 × 0,9 л |
| 5 | Краска интерьерная водно-дисперсионная акриловая для стен, полуматовая, класс мокрого истирания 1 по EN 13300, база A; цвет NCS S 1502-Y50R, колеровка машинная | Tikkurila | | Tikkurila | л | 7,2 | | поз. К8 колерной карты; пом. 5; S = 24,6 м² × 2 сл. × 0,12 л/м² = 5,9 л, +10 % и 0,5 л на подкраску → ≥ 7,0 л; тара 2 × 2,7 л + 2 × 0,9 л |
| 6 | Краска интерьерная водно-дисперсионная акриловая для стен, матовая, класс мокрого истирания 1 по EN 13300, база A; цвет Tikkurila V503 «Winter», колеровка машинная | Tikkurila Harmony | | Tikkurila | л | 7,2 | | поз. К9 колерной карты; пом. 6; S = 24,7 м² × 2 сл. × 0,12 л/м² = 5,9 л, +10 % и 0,5 л на подкраску → ≥ 7,0 л; тара 2 × 2,7 л + 2 × 0,9 л |
| 7 | Краска интерьерная водно-дисперсионная акриловая для потолков, глубокоматовая, класс мокрого истирания 2 по EN 13300, база A; цвет Tikkurila V503 «Winter», колеровка машинная | Tikkurila Anti-Reflex 2 | | Tikkurila | л | 2,7 | | поз. К10 колерной карты; пом. 6; S = 5,9 м² × 2 сл. × 0,12 л/м² = 1,4 л, +10 % и 0,5 л на подкраску → ≥ 2,1 л; тара 1 × 2,7 л |
| 8 | Акрил, полуматовая в цвет NCS S 0300-N — окраска плинтуса | аналог по характеристикам | | | л | 1,4 | | поз. К3; пом. 1, 2, 5; L = 39,9 м, S = 5,0 м² × 2 сл. × 0,12 л/м² + 10 %; продукт подобрать в веере NCS |
| 9 | Краска для МДФ и дерева в цвет Tikkurila V503 «Winter» — окраска плинтуса; блеск не ниже блеска стен | марка не задана | | | л | 0,5 | | поз. К11; пом. 6; L = 9,0 м, S = 1,1 м² × 2 сл. × 0,12 л/м² + 10 %; продукт подобрать в веере Tikkurila |
| 10 | Грунтовка акриловая под окраску стен и потолков — из системы производителя краски | по системе краски | | | м² | 184 | | площадь окраски стен, акцентов и потолков; 1 слой перед окраской; расход — по ТУ грунтовки |
| | **Плитка и керамогранит** | | | | | | | |
| 11 | SG651622R, 600×600 мм, противоскольжение R10 | SG651622R | | Kerama Marazzi | м² | 19,44 | | шов 2 мм; Ванная, пол; Санузел, пол; Прихожая, пол; по раскладке 48 шт (S = 14,30 м²), с запасом 54 шт |
| 12 | 610015000370, 600×1200 мм | 610015000370 | | Italon | м² | 19,41 | | 3. Ванная, стены; раскладка не выполнена — S = 17,64 м² + 10 %; клей и затирка — по раскладке |
| 13 | 610015000370, 600×1200 мм | 610015000370 | | Italon | м² | 16,19 | | 4. Санузел, стены; раскладка не выполнена — S = 14,71 м² + 10 %; клей и затирка — по раскладке |
| | **Напольные покрытия** | | | | | | | |
| 14 | IM1861, класс 33, рабочий слой 4 мм, эмиссия E1, укладка на клей | IM1861 | | Quick-Step | м² | 37,5 | | пом. 1, 2; S = 34,99 м² + 7 % (прямая укладка); к заказу — кратно упаковке |
| 15 | IM1861, рабочий слой 4 мм, эмиссия E1, укладка на клей | IM1861 | | Quick-Step | м² | 6,4 | | пом. 6; S = 5,94 м² + 7 % (прямая укладка); к заказу — кратно упаковке |
| 16 | Клей для паркета и инженерной доски, эластичный (СМП / полиуретановый) | по рекомендации производителя доски | | | м² | 41 | | площадь приклейки; расход и шпатель — по ТУ клея |
| | **Погонажные изделия** | | | | | | | |
| 17 | SX184, h = 110 мм, крепление к стене, окраска в цвет NCS S 0300-N | SX184 | | Orac Decor | м | 54 | | пом. 1, 2, 5, 6; L = 48,8 м (периметр без дверных проёмов) + 10 % на подрезку; в штуках — по длине планки |
| | **Смеси и материалы для облицовки** | | | | | | | |
| 18 | Затирка для швов плитки | аналог по характеристикам | | | кг | 1,5 | | по раскладке (a+b)/(a·b) × шов × t × 1,6 + 10 % |
| 19 | Клей плиточный C2 S1 по EN 12004, слой 5 мм | аналог по характеристикам | | | кг | 37 | | 2 меш. по 25 кг; 1,5 кг/м² на 1 мм слоя + 10 % |
| 20 | Клей плиточный C2 по EN 12004, слой 5 мм | аналог по характеристикам | | | кг | 78 | | 4 меш. по 25 кг; 1,5 кг/м² на 1 мм слоя + 10 % |
| 21 | Лента демпферная по периметру пола из плитки | аналог по характеристикам | | | м | 21,2 | | периметр без дверных проёмов + 10 % |

## Примечания

1. Количества — из геометрии проекта: площади поверхностей по чистым граням стен до отделки (те же, что в ведомости отделки и колерной карте), плитка, клей и затирка — по раскладке плиточника; в графе «Кол.» — к заказу, с запасом.
2. Краска: расход 0,12 л/м² на слой в 2 слоя, если по ТУ не задан иной; запас 10 % и 0,5 л на подкраску каждого кода. Один код — одна партия, колеровка машинная в колеровочном центре бренда; в заказ — только после утверждения выкраса (колерная карта). Фасовка — по каталогу бренда на дату выпуска; к заказу — не меньше расчётного объёма.
3. «Аналог по характеристикам» — допускается изделие другого производителя с характеристиками не ниже указанных, по согласованию с автором проекта.
4. Графы «Код продукции» и «Масса 1 ед.» не заполнены: коды по классификатору продукции не присвоены, масса единицы до 25 кг (ГОСТ 21.110-2013).
5. Грунтовка и клей для доски указаны площадью обработки; объём — по ТУ выбранного продукта.


| | | | | | |
|---|---|---|---|---|---|
| | | | | | Проект: Квартира 58 м² |
| | Лист | № док. | Подпись | Дата | Спецификация отделочных материалов |
| Дизайнер | Кырпан А.С. | | | 09.10.26 | |

| Стадия | Лист | Листов |
|---|---|---|
| П | С2 | 60 |

выпуск 09.10.2026 № 6e771c53bc · стр. 59 из 60


### 1 Порог 15 мм: мокрая зона — жилое помещение (М 1:5)

Применение: двери Д-4

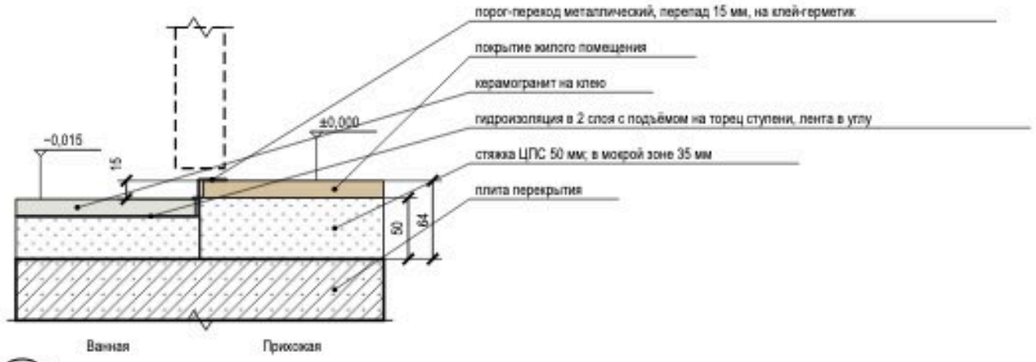



### 2 Дверь скрытого монтажа в плоскости стены, плинтус (М 1:5)

Применение: двери Д-2, Д-3, Д-4

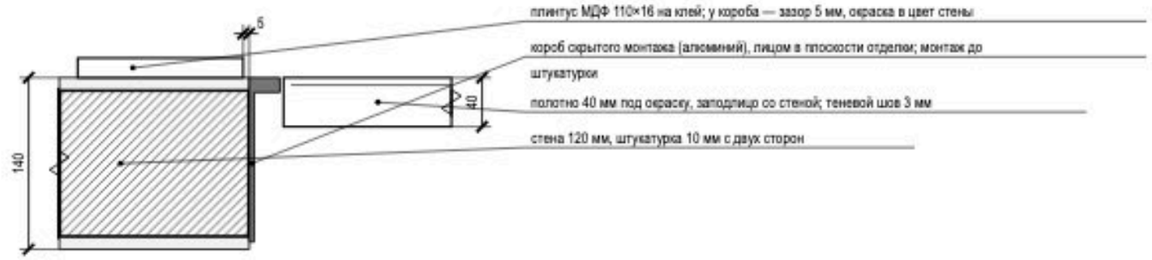



### 3 Короб стояков К1-1 с люком и звукоизоляцией (М 1:10)

Применение: пом. 3

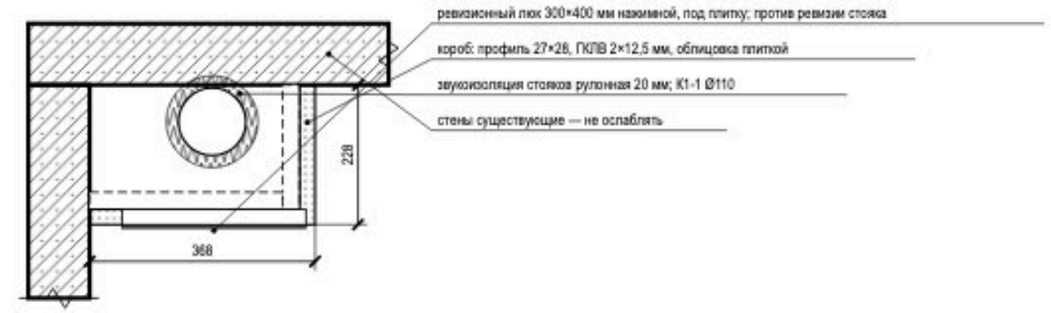



### 4 Гидроизоляция санузла: заход на стены 200 мм, примыкание ванны (М 1:20)

Применение: пом. 3, 4

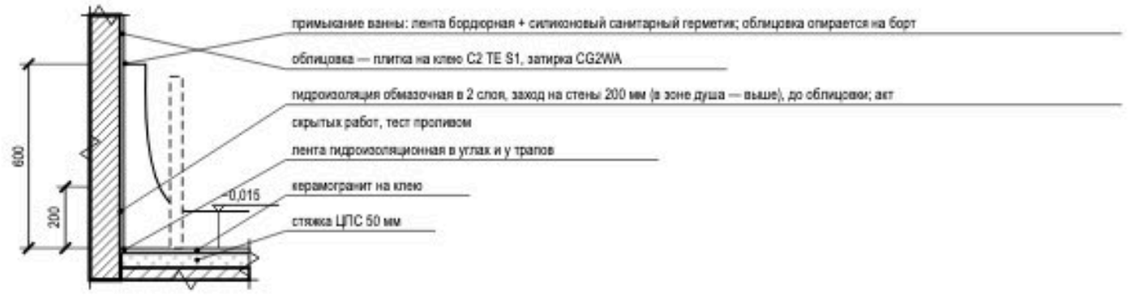


### 5 Плинтус МДФ 110×16 мм у окрашенной стены (М 1:10)

Применение: пом. 1, 2, 5, 6

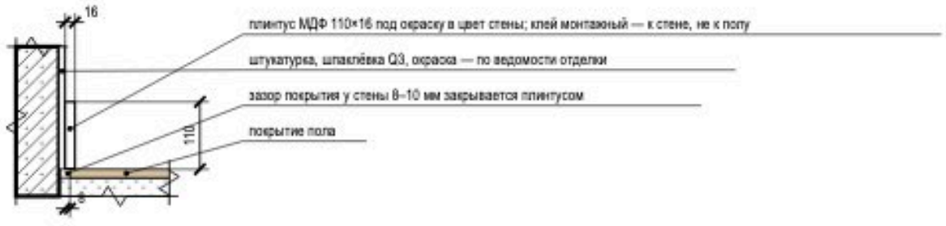


## Условные обозначения

- железобетон (плита, стены)
- кладка, перегородка
- стяжка, раствор
- гипсокартон ГКЛВ
- звукоизоляция, эластичный заполнитель
- плитка, керамогранит на клею
- инженерная доска (покрытие пола)
- металлический профиль (порог, Т-профиль, короб двери)
- гидроизоляция (обмазочная, лента)

## Примечания

1. Узлы — типовые решения проекта для мест, отмеченных выносками на листе схемы расположения развёрток и узлов; размеры — в мм, отметки — в м от ±0,000.
2. Узлы с гидроизоляцией, закладными и коробами скрытого монтажа принимаются по актам скрытых работ до закрытия отделкой; гидроизоляция — после теста проливом (24 ч).
3. Марки изделий (порог, Т-профиль, короб скрытой двери, люк) — по спецификациям; замена — на аналог с теми же габаритами по согласованию с автором проекта.

| | | | | | |
|---|---|---|---|---|---|
| | | | | | Проект: Квартира 58 м² |
| | Лист | № док. | Подпись | Дата | Узлы |
| Дизайнер | Кырпан А.С. | | | 09.10.26 | |

| Стадия | Лист | Листов |
|---|---|---|
| П | С3 | 60 |

выпуск 09.10.2026 № 6e771c53bc · стр. 60 из 60