ДИЗАЙН-ПРОЕКТ ИНТЕРЬЕРА

Четырёхкомнатная квартира

13 помещений

102,67 м²

актуальность · комфорт · мягкая геометрия · контраст фактур · открытость · уверенность

60 % — тёплый белый Paper F497 и песочный Castle J484, 30 % — грейж Claystone V486 в фасадах встроенного хранения и текстиле, 10 % — коричнево-лиловый Silhouette L481 из палитры стиля: ТВ-стена зала, изголовья детских, фасад кухонного острова. По практике тёплая аналоговая гамма ровнее держит цвет в квартире с окнами на разные стороны.

ПАЛИТРА 60 / 30 / 10

F497	J484	V486	L481
60 %	60 %	30 %	10 %

АВТОР ПРОЕКТА

Кырлан Александр Сергеевич

Октябрь 2026



В1 · Вид сверху (3D): планировка с мебелью, текстилем и декором

ОБЪЕКТ	ОБЩАЯ ПЛОЩАДЬ	ПОМЕЩЕНИЙ
Четырёхкомнатная квартира	102,67 м²	13, из них жилых 4
СТИЛЬ	**СТАДИЯ**	**ШИФР**
Современный (контемпорари) · 13 помещений	Рабочий проект	ГД-2026-004-АИ

	Лист	№ док.	Подпись	Дата	Проект: Четырёхкомнатная квартира			
Дизайнер	Кырлан А.С.			05.10.26	Титульный лист	Стадия	Лист	Листов
						П	1	111

выпуск 05.10.2026 № d0efc1af8a · стр. 1 из 111

Список листов

Лист	Наименование
1	Титульный лист
2	Список листов
3	План планировки от заказчика
4	План монтажный
5	Кухня (пом. 6). Монтажная схема
6	Кухня (пом. 6). Монтажная схема
7	Шкафы. Монтажная схема. Лист 1 из 3
8	Шкафы. Монтажная схема. Лист 2 из 3
9	Шкафы. Монтажная схема. Лист 3 из 3
10	Карта покрытий стен
11	Колерная карта
12	План размещения мебели и оборудования
13	Спецификация мебели и оборудования
14	Спецификация мебели и оборудования (продолжение)
15	Спецификация мебели и оборудования (продолжение)
16	Спецификация мебели и оборудования (продолжение)
17	Ведомости изделий, техники и фурнитуры
18	План выводов сантехники
19	Схема разводки водопровода и канализации
20	Спецификация сантехнического оборудования
21	Раскладка плитки. Ванная комната. Развёртки стен
22	Раскладка плитки. Санузел. Развёртки стен
23	План размещения дверей
24	План потолков
25	Разрезы и узлы потолков
26	План розеток и электровыводов
27	План слаботочных сетей
28	План освещения
29	Спецификация светильников и сценарии освещения
30	Управление светильниками
31	План вентиляции
32	План отопления
33	План покрытий пола
34	Раскладка плитки. Планы полов
35	Раскладка плитки. Фартук кухни
36	Визуализация. Вид сверху
37	Визуализация: Зал
38	Визуализация: Зал
39	Визуализация: Зал
40	Визуализация: Зал

Лист	Наименование
41	Развёртка стены А. Зал (пом. 1)
42	Развёртка стены Б. Зал (пом. 1)
43	Развёртка стены В. Зал (пом. 1)
44	Развёртка стены Г. Зал (пом. 1)
45	Визуализация: Ванная комната
46	Развёртки стен А, Б. Ванная комната (пом. 2)
47	Развёртки стен В, Г. Ванная комната (пом. 2)
48	Визуализация: Тёмная комната
49	Развёртки стен А, Б. Тёмная комната (пом. 3)
50	Развёртки стен В, Г. Тёмная комната (пом. 3)
51	Визуализация: Детская 1
52	Визуализация: Детская 1
53	Развёртка стены А. Детская 1 (пом. 4)
54	Развёртка стены Б. Детская 1 (пом. 4)
55	Развёртка стены В. Детская 1 (пом. 4)
56	Развёртка стены Г. Детская 1 (пом. 4)
57	Визуализация коридора
58	Визуализация коридора
59	Развёртки стен А, Б. Коридор (пом. 5)
60	Развёртка стены В. Коридор (пом. 5)
61	Визуализация кухни
62	Развёртка стены А. Кухня (пом. 6), кухонный фронт
63	Развёртка стены Б. Кухня (пом. 6)
64	Развёртка стены В. Кухня (пом. 6)
65	Развёртка стены Г. Кухня (пом. 6)
66	Визуализация: Прихожая-коридор
67	Развёртка стены А. Прихожая-коридор (пом. 7)
68	Развёртка стены Б. Прихожая-коридор (пом. 7)
69	Развёртка стены В. Прихожая-коридор (пом. 7)
70	Развёртка стены Г. Прихожая-коридор (пом. 7)
71	Визуализация: Гардеробная 2
72	Развёртки стен А, Б, В. Гардеробная 2 (пом. 8)
73	Развёртка стены Г. Гардеробная 2 (пом. 8)
74	Визуализация: Детская 2
75	Визуализация: Детская 2
76	Развёртка стены А. Детская 2 (пом. 9)
77	Развёртка стены Б. Детская 2 (пом. 9)
78	Развёртка стены В. Детская 2 (пом. 9)
79	Развёртка стены Г. Детская 2 (пом. 9)
80	Визуализация санузла

Лист	Наименование
81	Развёртки стен А, Б. Санузел (пом. 10)
82	Развёртки стен В, Г. Санузел (пом. 10)
83	Визуализация гостиной
84	Визуализация гостиной
85	Развёртка стены А. Гостиная (пом. 11)
86	Развёртка стены Б. Гостиная (пом. 11)
87	Развёртки стен В, Г. Гостиная (пом. 11)
88	Визуализация: Гардеробная 1
89	Развёртки стен А, Б. Гардеробная 1 (пом. 12)
90	Развёртка стены В. Гардеробная 1 (пом. 12)
91	Визуализация: Балкон 1
92	Развёртки стен А, Б. Балкон 1 (пом. 13)
93	Развёртки стен В, Г. Балкон 1 (пом. 13)
Д_1	Система хранения М_07
Д_2	Система хранения М_08
Д_3	Система хранения М_09
Д_4	Шкаф распашной М_15
Д_5	Система хранения М_17
Д_6	Система хранения М_18
Д_7	Шкаф-купе М_28
Д_8	Система хранения М_31
Д_9	Система хранения М_32
Д_10	Шкаф распашной М_34
Д_11	Система хранения М_38
Д_12	Система хранения М_39
Д_13	Система хранения М_40
Д_14	Кухня (пом. 6). Развёртка гарнитура
Д_15	Кухня (пом. 6). Развёртка гарнитура
С1	Ведомость отделки помещений. Лист 1 из 2
С2	Спецификация отделочных материалов
С3	Узлы


					Проект: Четырёхкомнатная квартира
	Лист	№ док.	Подпись	Дата	Список листов
Дизайнер	Карпан А.С.			05.10.26	

Стадия	Лист	Листов
П	2	111

выпуск 05.10.2026 · d0efc1af8a · стр. 2 из 111

Отметки по высоте

±0,000	чистый пол пом. 1, 3–9, 11, 12; отсчёт высот
−0,015	чистый пол пом. 2, 10, ниже на 15 мм
−0,030	чистый пол пом. 13, ниже на 30 мм
−0,170	верх плиты — расчёт, не замер (задание на обмер)
сущ. пол	снимается до плиты; не замерен (задание на обмер)

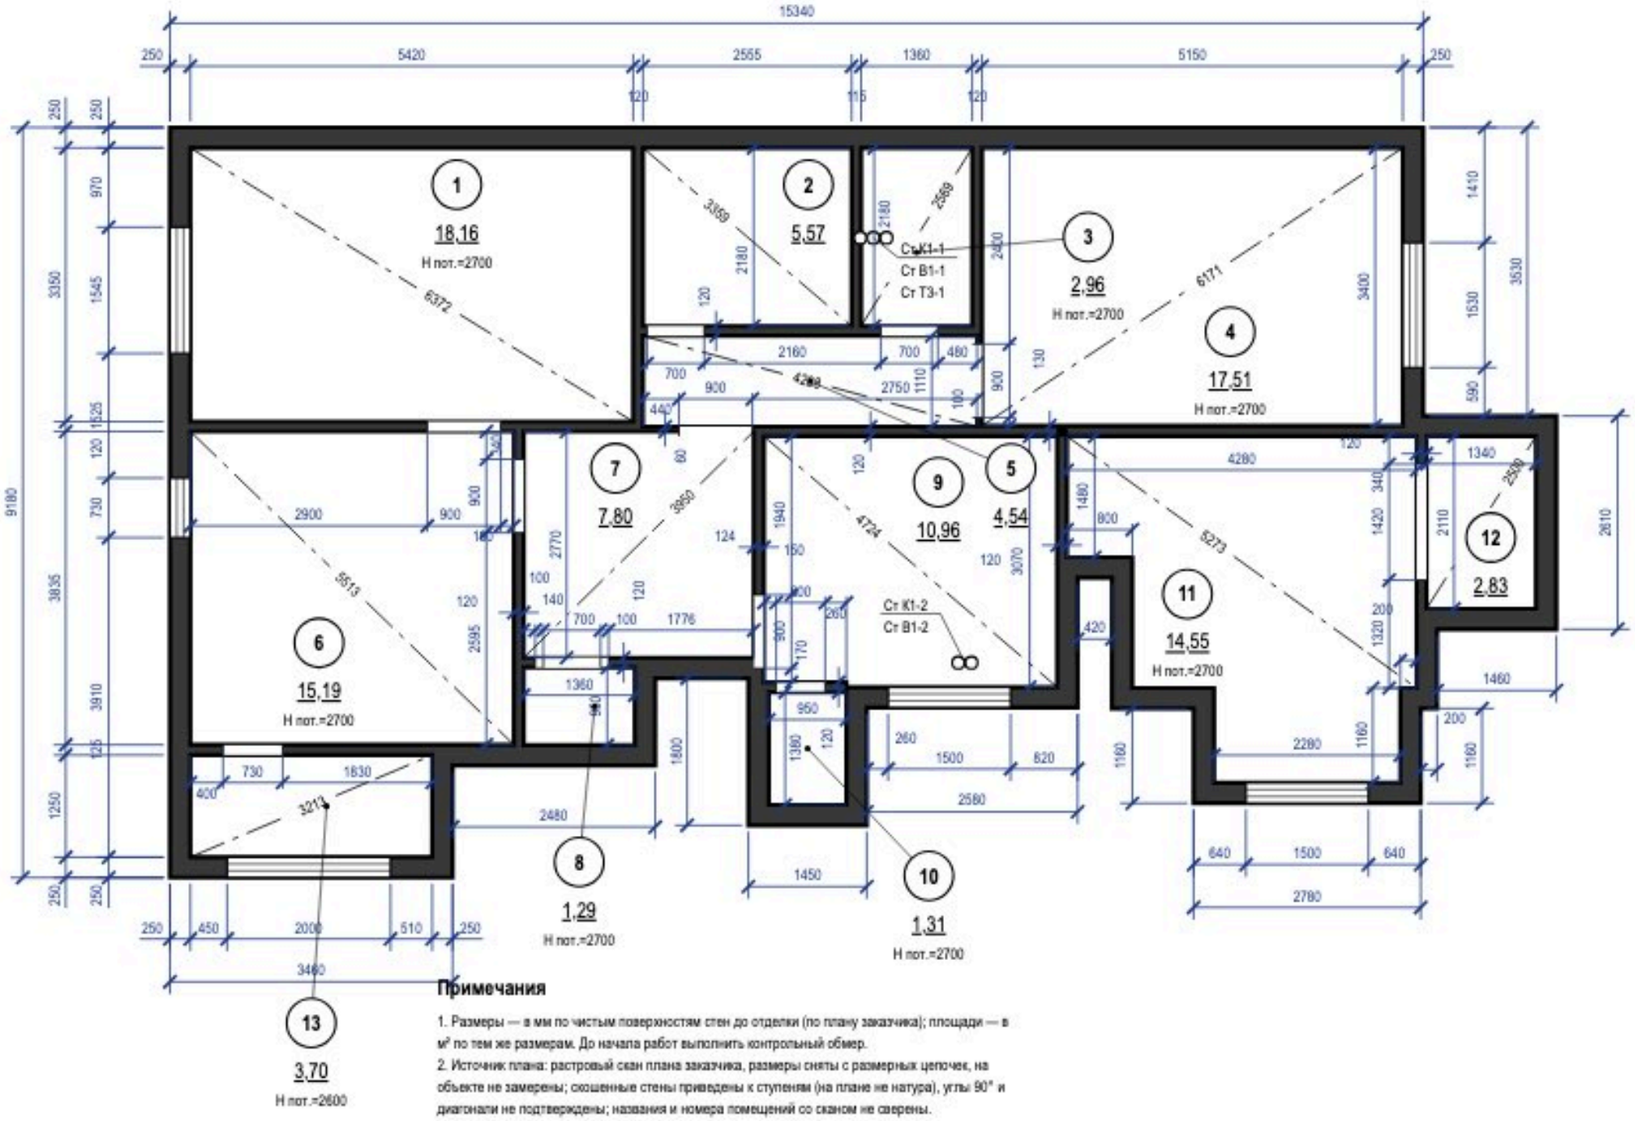

Экспликация помещений

№	Наименование	Площадь, м²
1	Зал	18,16
2	Ванная комната	5,57
3	Тёмная комната	2,96
4	Детская 1	17,51
5	Коридор	4,54
6	Кухня	15,19
7	Прихожая-коридор	7,80
8	Гардеробная 2	1,29
9	Детская 2	10,96
10	Санузел	1,31
11	Гостиная	14,55
12	Гардеробная 1	2,83
13	Балкон 1 *	3,70
	Итого (общая площадь)	**102,67**

Условные обозначения

- существующие стены (сечение)
- окно (рама, остекление)
- проём существующий, без заполнения (откосы)
- стояк: К1 — канализация, В1 — ХВС, Т3 — ГВС
- диагональ помещения — контроль прямоугольности
- (1) номер помещения, площадь м²


Примечания

1. Размеры — в мм по чистым поверхностям стен до отделки (по плану заказчика); площади — в м² по тем же размерам. До начала работ выполнить контрольный обмер.
2. Источник плана: растровый скан плана заказчика, размеры сняты с размерных цепочек, на объекте не замерены; скошенные стены приведены к ступеням (на плане не натура), углы 90° и диагонали не подтверждены; названия и номера помещений со сканом не сверены.
3. За отметку ±0,000 принят чистый пол, не существующий (блок отметок). Н пот. — высота от чистого пола до плиты перекрытия.
4. Толщины стен: наружные 250 мм, перегородки 120 мм; отличающиеся толщины и уступы размерами на плане.
5. Несущие стены не определены: до технического заключения все стены считать несущими; проёмы и штробы в них не выполнять.
6. Дверные проёмы показаны без заполнения (двери — лист 23); высота дверных проёмов 2100 мм; низ окон (подоконник) 800, 900 мм от чистого пола, высота окон 1600, 1700 мм.
7. Диагонали — контрольные размеры; расхождение более 5 мм подписать на плане как перекос.
8. Размеры проверить на месте до начала работ; расхождение контрольных промеров ≤ 2 %.
9. Помещения, отмеченные *, в общую площадь квартиры не входят.
10. Размеры короче 1 мм на листе цепочкой не показаны (две выносные линии на таком расстоянии сливаются): пом. 5, стена А — 50 мм от угла до проёма.

					Проект: Четырёхкомнатная квартира
	Лист	№ док.	Подпись	Дата	План планировки от заказчика
Дизайнер	Кырпан А.С.			05.10.26	

Стадия	Лист	Листов
П	3	111

выпуск 05.10.2026 · d0efc1af8a · стр. 3 из 111

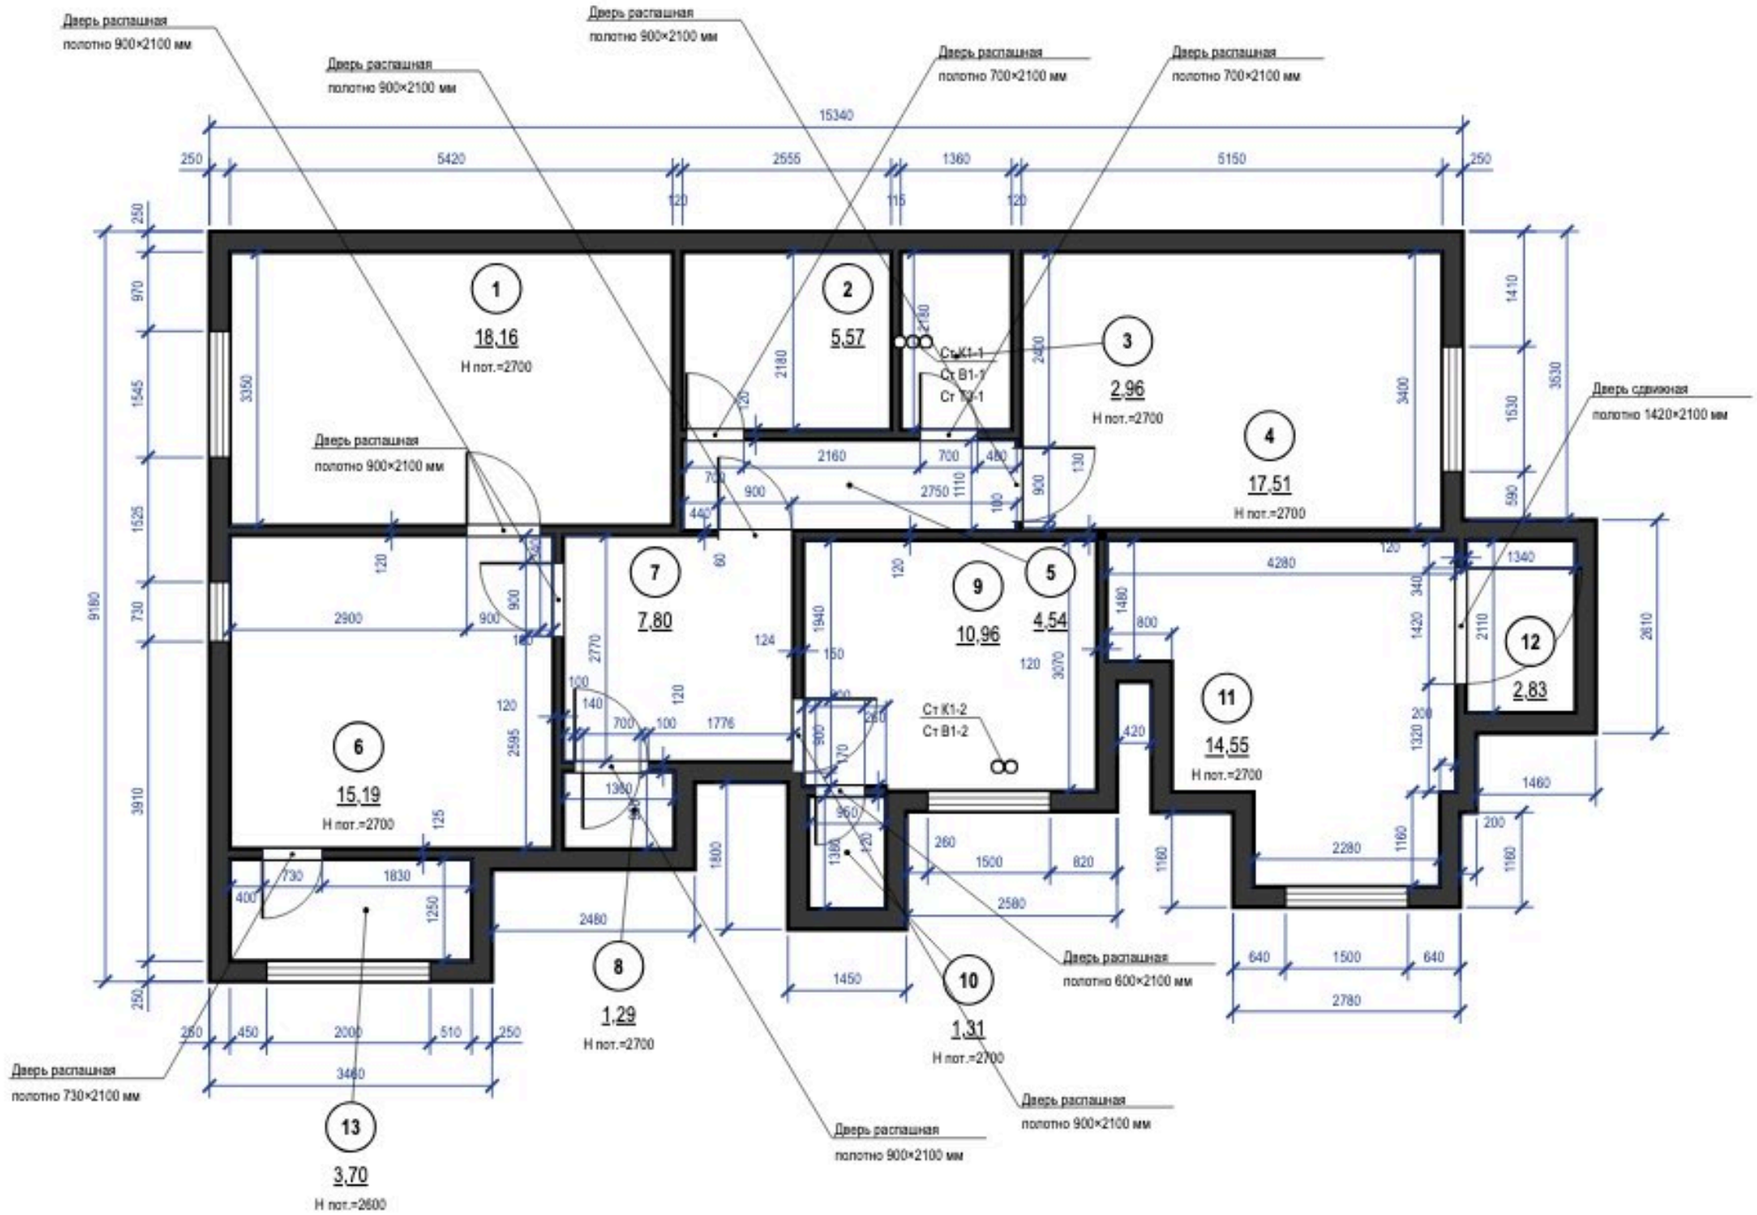

Экспликация помещений

№	Наименование	Площадь, м²
1	Зал	18,16
2	Ванная комната	5,57
3	Тёмная комната	2,96
4	Детская 1	17,51
5	Кормдор	4,54
6	Кухня	15,19
7	Прихожая-коридор	7,80
8	Гардеробная 2	1,29
9	Детская 2	10,96
10	Санузел	1,31
11	Гостиная	14,55
12	Гардеробная 1	2,83
13	Балкон 1 *	3,70
	Итого (общая площадь)	**102,67**

Примечания


1. Размеры — в мм от чистовых поверхностей стен до отделки; размеры уточнить по месту до начала работ.
2. Новые перегородки и облицовки — синим; каркас и обшивка — по выноскам; двери и проёмы лист 23.
3. Несущие стены не изменять: проёмы, ниши и штробы в них — только по техническому заключению.
4. Размеры короче 1 мм на листе цепочкой не показаны (две выносные линии на таком расстоянии сливаются): пом. 5, стена А — 50 мм от угла до проёма.

					Проект: Четырёхкомнатная квартира
	Лист	№ док.	Подпись	Дата	
Дизайнер	Кырпан А.С.			05.10.26	План монтажный

Стадия	Лист	Листов
П	4	111

выпуск 05.10.2026 № d0efc1af8a · стр. 4 из 111

Привязка выводов и крепление модулей

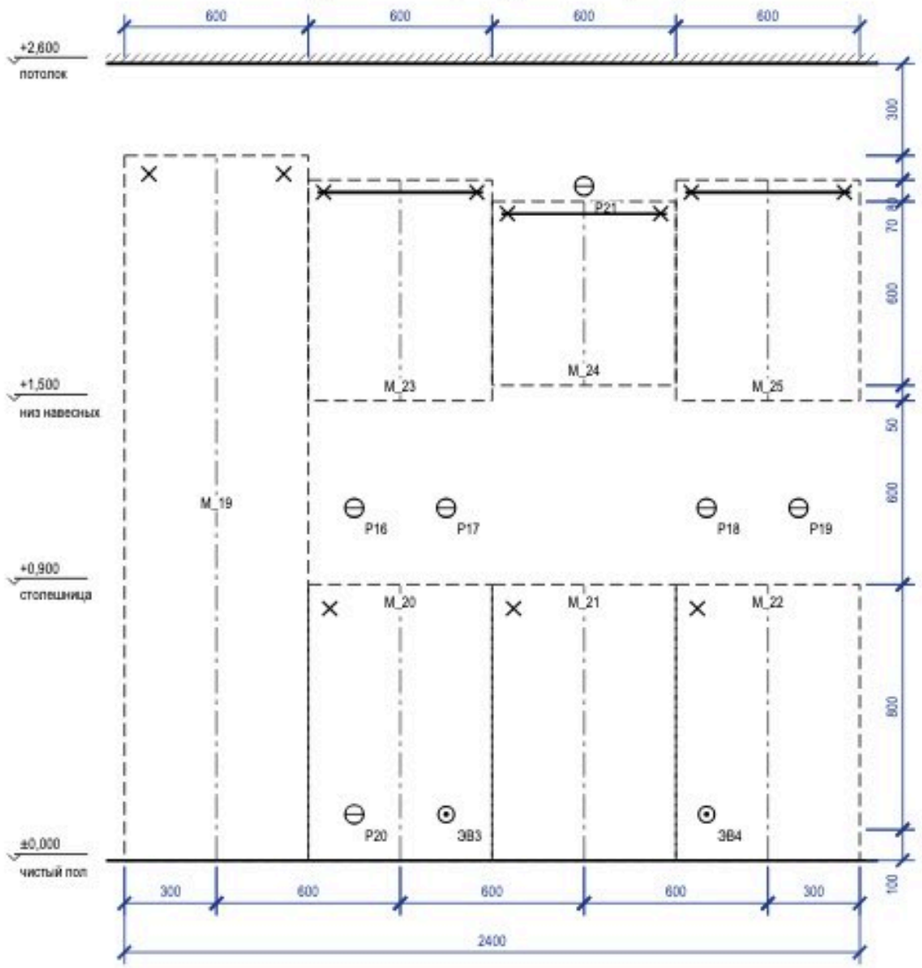

План столешницы



Привязка выводов к осям модулей

Код	Назначение	Модуль	От оси, мм	H, мм	Размещение
P16	розетка ×2 — фартук: мелкая техника	M_20	−150	1150	над столешницей (фартук)
P20	розетка — холодильник встроенный M_19 (розетка в модуле M_20)	M_20	−150	150	в соседнем модуле, за ящиком
P17	розетка ×2 — фартук: мелкая техника	M_20	+150	1150	над столешницей (фартук)
ЭВ3	вывод кабеля — варочная панель M_21	M_20	+150	150	в соседнем модуле, за ящиком
P21	розетка — вытяжка M_24 (в модуле, съёмная панель)	M_24	0	2200	в навесном модуле
P18	розетка ×2 — фартук: мелкая техника	M_22	−200	1150	над столешницей (фартук)
ЭВ4	вывод кабеля — духовой шкаф M_21 (вывод в соседнем модуле M_22)	M_22	−200	150	в соседнем модуле, за ящиком
P19	розетка ×2 — фартук: мелкая техника	M_22	+100	1150	над столешницей (фартук)

Зазоры под отделку

Поверхность	Отделка	Зазор, мм	Учесть
фартук	керамогранит	10	от чернового основания до корпуса навесных и столешницы
стены	окраска	5	под штукатурку и шпаклёвку за пеналом
пол	инженерная доска		цоколь — после укладки пола, опоры ±20 мм

Условные обозначения

- навесной модуль (невидимый контур)
- ось модуля (от неё — привязка вывода)
- анкер / уголок крепления к стене
- розетка на стене
- вывод кабеля к технике
- B1 — вывод воды B1 / Т3, канализации К1

Примечания


1. Выводы — по проекту электрики и ВК; привязка по горизонтали — от оси модуля (плюс — вправо по виду), по высоте — от чистого пола до оси вывода.
2. Пенал — уголки к стене 2 шт. сверху; нижние модули — стяжками между собой и уголком к стене; ряд выставить по уровню опорами цоколя.
3. Розетки над столешницей — не ниже 150 мм над ней и не за корпусом техники; розетка за ПММ, духовым шкафом и холодильником — только в соседнем модуле или в зоне цоколя с доступом.
4. Столешница — вырезы по шаблонам выбранных моделей мойки и варочной панели; торцы у стены — герметик, пристеночный плинтус.

					Проект: Четырёхкомнатная квартира
	Лист	№ док.	Подпись	Дата	Кухня (пом. 6). Монтажная схема
Дизайнер	Кырпан А.С.			05.10.26	

Стадия	Лист	Листов
П	5	111

выпуск 05.10.2026 № d0efc1af8a · стр. 5 из 111

Привязка выводов и крепление модулей

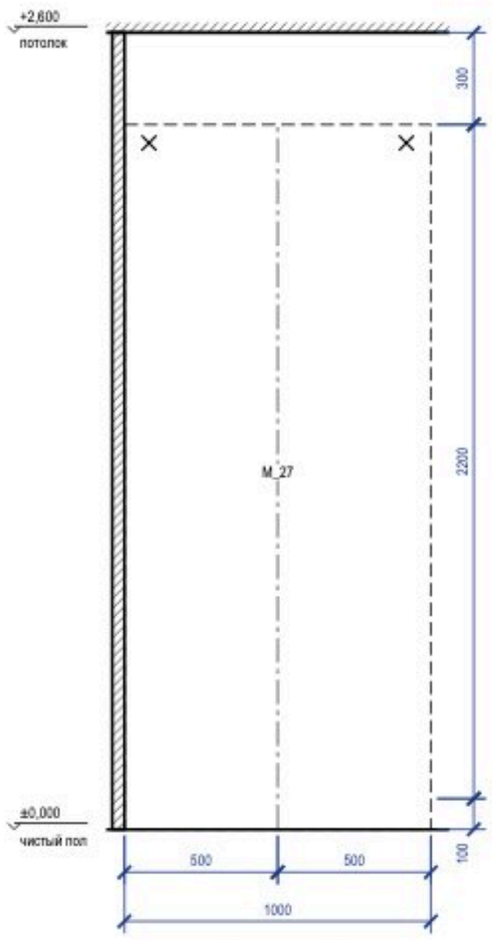

Привязка выводов к осям модулей

Код	Назначение	Модуль	От оси, мм	H, мм	Размещение

Зазоры под отделку

Поверхность	Отделка	Зазор, мм	Учесть
фартук	керамогранит	10	от чернового основания до корпуса навесных и столешницы
стены	окраска	5	под штукатурку и шпаклёвку за пеналом
пол	инженерная доска		цоколь — после укладки пола, опоры ±20 мм

Условные обозначения

- навесной модуль (невидимый контур)
- ось модуля (от неё — привязка вывода)
- анкер / уголок крепления к стене
- розетка на стене
- вывод кабеля к технике
- В1 — вывод воды В1 / Т3, канализации К1

Примечания


1. Выводы — по проекту электрики и ВК; привязка по горизонтали — от оси модуля (плюс — вправо по виду), по высоте — от чистого пола до оси вывода.
2. Пенал — уголки к стене 2 шт. сверху; нижние модули — стяжками между собой и уголком к стене; ряд выставить по уровню опорами цоколя.
3. Розетки над столешницей — не ниже 150 мм над ней и не за корпусом техники; розетка за ПММ, духовым шкафом и холодильником — только в соседнем модуле или в зоне цоколя с доступом.
4. Столешница — вырезы по шаблонам выбранных моделей мойки и варочной панели; торцы у стены — герметик, пристеночный плинтус.

					Проект: Четырёхкомнатная квартира
	Лист	№ док.	Подпись	Дата	Кухня (пом. 6). Монтажная схема
Дизайнер	Кырпан А.С.			05.10.26	


Стадия	Лист	Листов
П	6	111

выпуск 05.10.2026 № d0efc1af8a · стр. 6 из 111


М_07 (пом. 2)

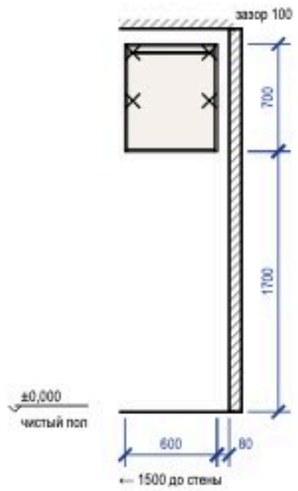


Система хранения М_08 (пом. 3)

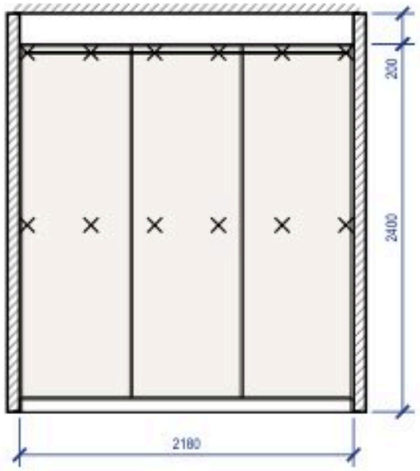


Система хранения М_09 (пом. 3)

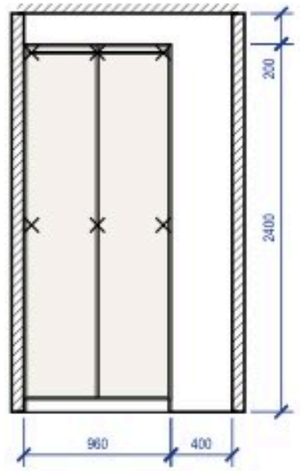

Шкаф распашной М_15 (пом. 4)

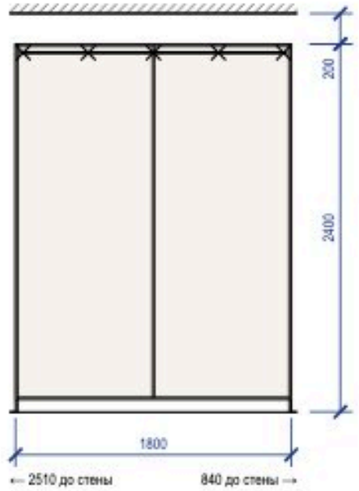

Система хранения М_17 (пом. 4)

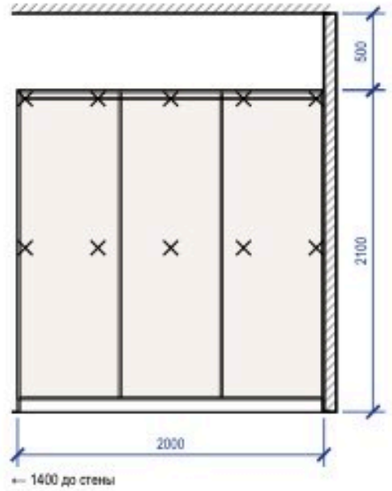

Крепление и зазоры под отделку (изделия листа 1)

Марка	Помещение, стена	Основание	Отделка стены	Зазор, мм	Крепёж по плане	От опрокидывания
М_07	Ванная комната (2), стена Б	по основанию — см. таблицу крепежа	плитка	10	анкер 4 шт. (2 ряда)	крепление к стене, 2 точки
М_08	Тёмная комната (3), стена Б	по основанию — см. таблицу крепежа	окраска	5	анкер 12 шт. (2 ряда)	крепление к стене, 4 точки
М_09	Тёмная комната (3), стена А	по основанию — см. таблицу крепежа	окраска	5	анкер 6 шт. (2 ряда)	крепление к стене, 3 точки
М_15	Детская 1 (4), стена В	по основанию — см. таблицу крепежа	окраска	5	анкер 5 шт., шаг 425	уголок к стене, 3 шт.
М_17	Детская 1 (4), стена Г	по основанию — см. таблицу крепежа	окраска	5	анкер 10 шт. (2 ряда)	крепление к стене, 3 точки

Крепёж по основанию стены

Основание стены	Крепёж
бетон, ж/б	анкер-шуруп 7,5×72 или дюбель 8×60 с шурупом 5×70
кирпич полнотелый	дюбель 8×80 с шурупом 5×90
газобетон, пазогребень	дюбель для газобетона 10×100 или химический анкер
гипсокартон	закладная до обшивки (брус 40×80 или фанера 18 мм), саморез в закладную

Условные обозначения

- × — анкер / уголок крепления к стене
- ▭ — корпус и полки ЛДСП (вид на стену)
- ▨ — компенсатор — короб до потолка


Примечания

1. Установочные размеры — от чистого пола и чистых стен; перед установкой контрольный замер после отделки.
2. Порядок: корпус выставить по уровню опорами цоколя → закрепить к стене по задней планке → навесить двери и фасады, отрегулировать зазоры → подогнать и закрепить компенсатор.
3. Анкеры — с шагом не более 500 мм, не ближе 50 мм от края планки; на ГКЛ только в закладную, установленную до обшивки.
4. Скрытые коммуникации под анкеры проверить детектором; трассы электрики по плану розеток.
5. Монтажная схема на 3 листах, лист 1 из 3; продолжение — на следующем листе схемы. Условные обозначения, таблица крепежа по основанию и примечания повторены на каждом листе.


					Проект: Четырёхкомнатная квартира	
	Лист	№ док.	Подпись	Дата		
Дизайнер	Кырпан А.С.			05.10.26	Шкафы. Монтажная схема. Лист 1 из 3	Стадия: П; Лист: 7; Листов: 111

выпуск 05.10.2026 · d0efc1af8a · стр. 7 из 111


Система хранения M_18 (пом. 5)

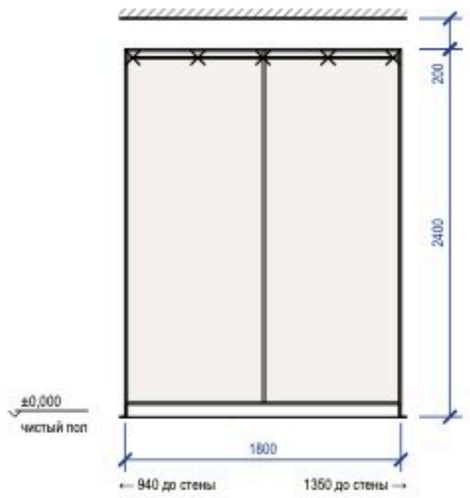


Шкаф-купе M_28 (пом. 7)

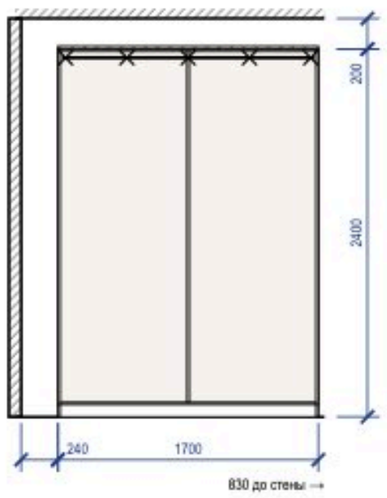


Система хранения M_31 пом. 8

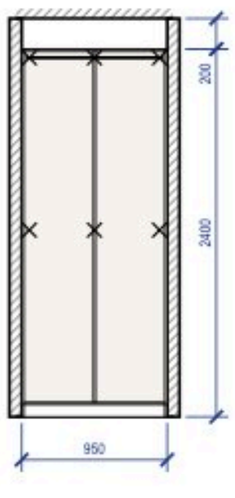

Система хранения M_32 (пом. 8)

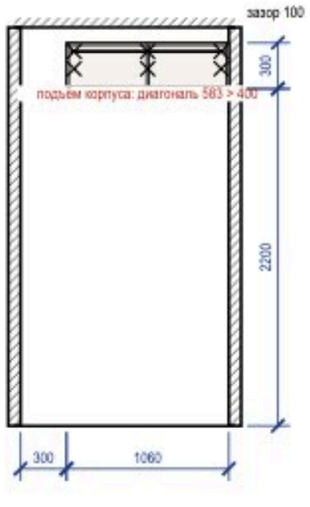

Шкаф распашной M_34 (пом. 9)

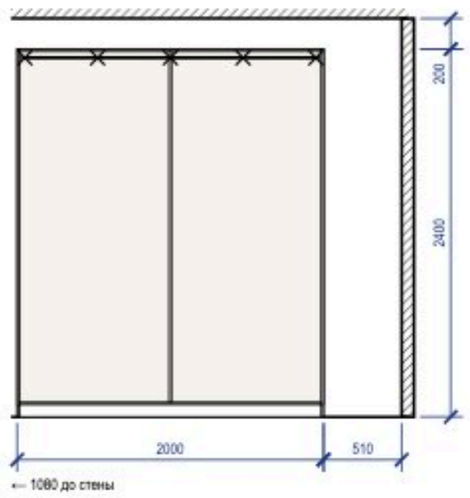

Крепление и зазоры под отделку (изделия листа 2)

Марка	Помещение, стена	Основание	Отделка стены	Зазор, мм	Крепёж по плане	От опрокидывания
M_18	Коридор (5), стена А	по основанию — см. таблицу крепежа	окраска	5	анкер 5 шт., шаг 425	крепление к стене, 4 точки
M_28	Прихожая-коридор (7), стена Б	по основанию — см. таблицу крепежа	окраска	5	анкер 5 шт., шаг 400	крепление к стене, 3 точки
M_31	Гардеробная 2 (8), стена Б	по основанию — см. таблицу крепежа	окраска	5	анкер 6 шт. (2 ряда)	крепление к стене, 3 точки
M_32	Гардеробная 2 (8), стена В	по основанию — см. таблицу крепежа	окраска	5	анкер 6 шт. (2 ряда)	крепление к стене, 4 точки
M_34	Детская 2 (9), стена А	по основанию — см. таблицу крепежа	окраска	5	анкер 5 шт., шаг 475	уголок к стене, 3 шт.

Крепёж по основанию стены

Основание стены	Крепёж
бетон, ж/б	анкер-шуруп 7,5×72 или дюбель 8×60 с шурупом 5×70
кирпич полнотелый	дюбель 8×80 с шурупом 5×90
газобетон, пазогребень	дюбель для газобетона 10×100 или химический анкер
гипсокартон	закладная до обшивки (брус 40×80 или фанера 18 мм), саморез в закладную

Условные обозначения

- × — анкер / уголок крепления к стене
- ▭ — корпус и полки ЛДСП (вид на стену)
- ▨ — компенсатор — короб до потолка


Примечания

1. Установочные размеры — от чистого пола и чистых стен; перед установкой контрольный замер после отделки.
2. Порядок: корпус выставить по уровню опорами цоколя → закрепить к стене по задней планке → навесить двери и фасады, отрегулировать зазоры → подогнать и закрепить компенсатор.
3. Анкеры — с шагом не более 500 мм, не ближе 50 мм от края планки; на ГКЛ только в закладную, установленную до обшивки.
4. Скрытые коммуникации под анкеры проверить детектором; трассы электрики по плану розеток.
5. Монтажная схема на 3 листах, лист 2 из 3; продолжение — на следующем листе схемы. Условные обозначения, таблица крепежа по основанию и примечания повторены на каждом листе.


					Проект: Четырёхкомнатная квартира	
	Лист	№ док.	Подпись	Дата		
Дизайнер	Кырпан А.С.			05.10.26	Шкафы. Монтажная схема. Лист 2 из 3	Стадия: П; Лист: 8; Листов: 111

выпуск 05.10.2026 · d0efc1af8a · стр. 8 из 111


Система хранения М_38 (пом. 12)

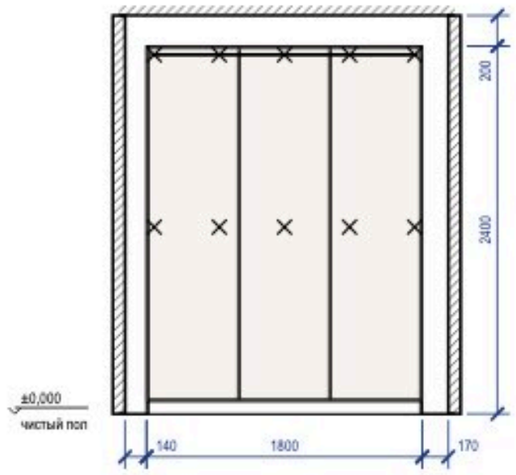

Система хранения М_39 пом. 13

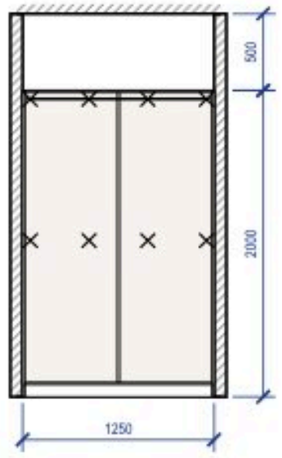

Система хранения М_40 пом. 13

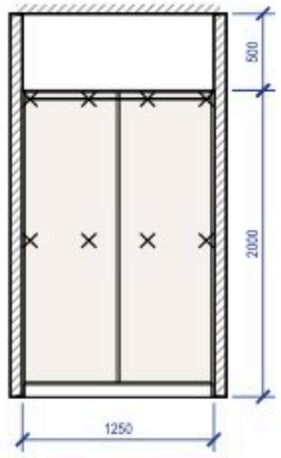

Крепление и зазоры под отделку (изделия листа 3)

Марка	Помещение, стена	Основание	Отделка стены	Зазор, мм	Крепёж по плане	От опрокидывания
М_38	Гардеробная 1 (12), стена Б	по основанию — см. таблицу крепежа	окраска	5	анкер 10 шт. (2 ряда)	крепление к стене, 4 точки
М_39	Балкон 1 (13), стена Б	по основанию — см. таблицу крепежа	окраска	5	анкер 8 шт. (2 ряда)	крепление к стене, 3 точки
М_40	Балкон 1 (13), стена Г	по основанию — см. таблицу крепежа	окраска	5	анкер 8 шт. (2 ряда)	крепление к стене, 3 точки

Крепёж по основанию стены

Основание стены	Крепёж
бетон, ж/б	анкер-шуруп 7,5×72 или дюбель 8×60 с шурупом 5×70
кирпич полнотелый	дюбель 8×80 с шурупом 5×90
газобетон, пазогребень	дюбель для газобетона 10×100 или химический анкер
гипсокартон	закладная до обшивки (брус 40×80 или фанера 18 мм), саморез в закладную

Условные обозначения

- × — анкер / уголок крепления к стене
- ▭ — корпус и полки ЛДСП (вид на стену)
- ▨ — компенсатор — короб до потолка

Примечания

1. Установочные размеры — от чистого пола и чистых стен; перед установкой контрольный замер после отделки.
2. Порядок: корпус выставить по уровню опорами цоколя → закрепить к стене по задней планке → навесить двери и фасады, отрегулировать зазоры → подогнать и закрепить компенсатор.
3. Анкеры — с шагом не более 500 мм, не ближе 50 мм от края планки; на ГКЛ только в закладную, установленную до обшивки.
4. Скрытые коммуникации под анкеры проверить детектором; трассы электрики по плану розеток.
5. Монтажная схема на 3 листах, лист 3 из 3. Условные обозначения, таблица крепежа по основанию и примечания повторены на каждом листе.

					Проект: Четырёхкомнатная квартира	
	Лист	№ док.	Подпись	Дата		
Дизайнер	Кырпан А.С.			05.10.26	Шкафы. Монтажная схема. Лист 3 из 3	Стадия: П; Лист: 9; Листов: 111

выпуск 05.10.2026 · d0efc1af8a · стр. 9 из 111



Покрытия стен

Марка	Покрытие	Помещение: S, м²	Итого, м²
O1	окраска Tikkurila · F497 «Paper»	1: 25,7; 3: 16,6; 8: 8,3; 11: 25,5; 12: 14,6	90,8
O2	окраска Tikkurila · L481 «Silhouette»	1: 13,5; 11: 10,6	24,1
O6	облицовка плиткой · «ton Paper F497» 600×600 мм	2: 21,9; 10: 10,0	31,8
O9	окраска Tikkurila · F497 «Paper»	4: 39,8; 9: 28,8	68,6
O10	окраска Tikkurila · J484 «Castle»	5: 20,0; 7: 20,0	40,0
O13	окраска Tikkurila · F497 «Paper»	6: 32,6; 13: 16,2	48,8

					Проект: Четырёхкомнатная квартира
	Лист	№ док.	Подпись	Дата	
Дизайнер	Кырпан А.С.			05.10.26	Карта покрытий стен

Стадия	Лист	Листов
П	10	111

Площади — нетто, по развёрткам (за вычетом проёмов и фартука); высоты помещений — от чистого пола.

выпуск 05.10.2026 № d0efc1af8a · стр. 10 из 111

Колерная карта по помещениям

Помещение	Поверхность	Образец	Поз.	Система и код цвета	Производитель, линейка / материал, артикул	Блеск	Класс EN 13300	LRV	Площадь
1. Зал 18,16 м²	стены		**K1**	Tikkurila F497	Tikkurila · Optiva 5 Matt	матовая	2	88	25,9 м²
	акцент А		**K2**	Tikkurila L481	Tikkurila · Optiva 5 Matt	матовая	2	18	13,6 м²
	потолок		**K3**	Tikkurila F497	Tikkurila · Anti-Reflex 2	глубокомат.	2	88	18,2 м²
	пол		**KM1**	по образцу	инженерная доска · аналог по хар.				18,2 м²
	плинтус		**K4**	Tikkurila F497	МДФ · в цвет Tikkurila	полуглянц.	2	88	16,6 м
2. Ванная комната 5,57 м²	стены		**KM2**	тон Paper F497 (тёплый белый)	плитка · аналог по хар.				22,3 м²
	потолок		**K5**	Tikkurila F497	Tikkurila · Luja 7	матовая	1	88	5,6 м²
	пол		**KM3**	тон Castle J484 (тёплый песочный)	керамогранит · аналог по хар.				5,6 м²
3. Тёмная комната 2,96 м²	стены		**K1**	Tikkurila F497	Tikkurila · Optiva 5 Matt	матовая	2	88	16,9 м²
	потолок		**K3**	Tikkurila F497	Tikkurila · Anti-Reflex 2	глубокомат.	2	88	3,0 м²
	пол		**KM1**	по образцу	инженерная доска · аналог по хар.				3,0 м²
	плинтус		**K4**	Tikkurila F497	МДФ · в цвет Tikkurila	полуглянц.	2	88	6,4 м
4. Детская 1 17,51 м²	стены		**K6**	Tikkurila F497	Tikkurila · Joker	полуматов.	2	88	40,1 м²
	потолок		**K3**	Tikkurila F497	Tikkurila · Anti-Reflex 2	глубокомат.	2	88	17,5 м²
	пол		**KM1**	по образцу	инженерная доска · аналог по хар.				17,5 м²
	плинтус		**K4**	Tikkurila F497	МДФ · в цвет Tikkurila	полуглянц.	2	88	16,2 м
5. Коридор 4,54 м²	стены		**K7**	Tikkurila J484	Tikkurila · Optiva 20 Semimatt	полуматов.	2	55	22,2 м²
	потолок		**K3**	Tikkurila F497	Tikkurila · Anti-Reflex 2	глубокомат.	2	88	4,5 м²
	пол		**KM4**	тон Claystone V486 (грейж)	керамогранит · аналог по хар.				4,5 м²
	плинтус		**K8**	Tikkurila J484	МДФ · в цвет Tikkurila	полуглянц.	2	55	8,1 м
6. Кухня 15,19 м²	стены		**K9**	Tikkurila F497	Tikkurila · Luja 7	полуматов.	1	88	34,5 м²
	потолок		**K5**	Tikkurila F497	Tikkurila · Luja 7	матовая	1	88	15,2 м²
	пол		**KM1**	по образцу	инженерная доска · аналог по хар.				15,2 м²
	плинтус		**K4**	Tikkurila F497	МДФ · в цвет Tikkurila	полуглянц.	2	88	13,8 м
	фартук		**KM5**	тон Paper F497 (тёплый белый)	керамогранит · аналог по хар.				1,1 м²

Схема палитры проекта


Стиль: Современный (контемпорари) · схема: аналоговая

основной	основной	второстепенный	акцентный
Tikkurila F497	**Tikkurila J484**	**Tikkurila V486**	**Tikkurila L481**
Paper LRV 88 стены 1,3,4,6,8,9,11,12,13; потолок 1,2,3,4,5,6,7,8,9,10,11,12,13; плинтус 1,3,4,6,8,9,11,12; текстиль/декор 1	Castle LRV 55 стены 5,7; плинтус 5,7; текстиль/декор 1,6	Claystone LRV 44 текстиль/декор 1,13	Silhouette LRV 18 акцент 1,11; текстиль/декор 1,11

План 60/30/10



Окраска, факт — по площади стен, акцентов, потолков

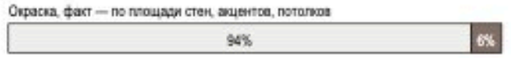

окрашено всего 389,8 м²; второстепенный тон несут мебель и текстиль

Текстиль и декор в цветах вне палитры проекта

- NCS S 3005-Y20R тёплый тауп-серый — пом. 1 (T3), 7 (T15), 9 (T18)
- Tikkurila H487 Pumice — пом. 1 (T4), 4 (T9, T10, T11), 9 (T17, T19)
- Tikkurila V484 Driftwood — пом. 4 (T8), 9 (T16), 13 (T23)
- NCS S 5010-B10G сero-петроль — пом. 4 (T12, T13)
- Farrow & Ball No. 47 Green Smoke — пом. 9 (T20, T21)

Условные обозначения

- **K1** Tikkurila F497 · Paper · Optiva 5 Matt · матовая · кл. 2
- **K2** Tikkurila L481 · Silhouette · Optiva 5 Matt · матовая · кл. 2
- **K3** Tikkurila F497 · Paper · Anti-Reflex 2 · глубокомат. · кл. 2
- **K4** Tikkurila F497 · Paper · МДФ · полуглянц. · кл. 2
- **K5** Tikkurila F497 · Paper · Luja 7 · матовая · кл. 1
- **K6** Tikkurila F497 · Paper · Joker · полуматов. · кл. 2
- **K7** Tikkurila J484 · Castle · Optiva 20 Semimatt · полуматов. · кл. 2
- **K8** Tikkurila J484 · Castle · МДФ · полуглянц. · кл. 2
- **K9** Tikkurila F497 · Paper · Luja 7 · полуматов. · кл. 1
- дерево (доска, паркет, ламинат) — рисунок досок
- керамогранит, плитка, камень — сетка швов по формату

- **KM1** инженерная доска · аналог: дуб натуральный брашированный, масло-воск, 14/4 мм
- **KM2** плитка · аналог: керамогранит матовый, тон F497, 600×600×9 мм
- **KM3** аналог: керамогранит матовый R10, тон J484, 600×600×10 мм
- **KM4** аналог: керамогранит матовый R10, тон V486, 600×600×10 мм
- **KM5** аналог: керамогранит матовый, тон F497, 600×600×9 мм
- **KM6** аналог: керамогранит матовый R11, тон V486, 600×600×10 мм
- **KM7** керамогранит · аналог: плинтус из керамогранита пола, подрезка 80 мм, верхняя кромка с затилом 45°

K — позиция окраски (код + продукт + блеск), KM — позиция материала, тон KM — по описанию артикула, эталон — образец материала; ≈ LRV — расчёт по HEX, справочно


Примечания

1. Цвет утверждается только по выкрасу на объекте: формат от А3 до 1000×1000 мм на загрунтованном ГКЛ, в 2 слоя (как на стене), не на белой шпаклёвке; смотреть днём и при свете проекта своего помещения, рядом с образцами пола и фасадов. Подпись на обороте: код, бренд и веер, дата.
2. Колеровка машинная в колеровочном центре бренда; каждый код — за один проход, одной партией на весь объём. Колеровщику передаётся только система и код утверждённого веера; плашки и HEX на листе — ориентир, печать не является эталоном цвета.
3. Класс мокрого истирания — EN 13300 (ISO 11998); блеск — по ГОСТ 31975 (ISO 2813), геометрия 60°. LRV — пересчёт координаты L каталога производителя ($Y = ((L^*+16)/116)^3$); «≈» — расчёт по HEX, справочно.
4. Площади поверхностей — тем же способом и с теми же цифрами, что в ведомости отделки (способ счёта — в общих указаниях); объём краски к заказу, фасовка и материалы KM — в спецификации отделочных материалов.
5. Колерная карта на 2 листах: обозначения повторены на каждом, схема квартиры и палитра — на первом, перечень выкрасов — на последнем.

					Проект: Четырёхкомнатная квартира
	Лист	№ док.	Подпись	Дата	Колерная карта
Дизайнер	Кырпан А.С.			05.10.26	

Стадия	Лист	Листов
П	11	111

выпуск 05.10.2026 · d0efc1af8a · стр. 11 из 111

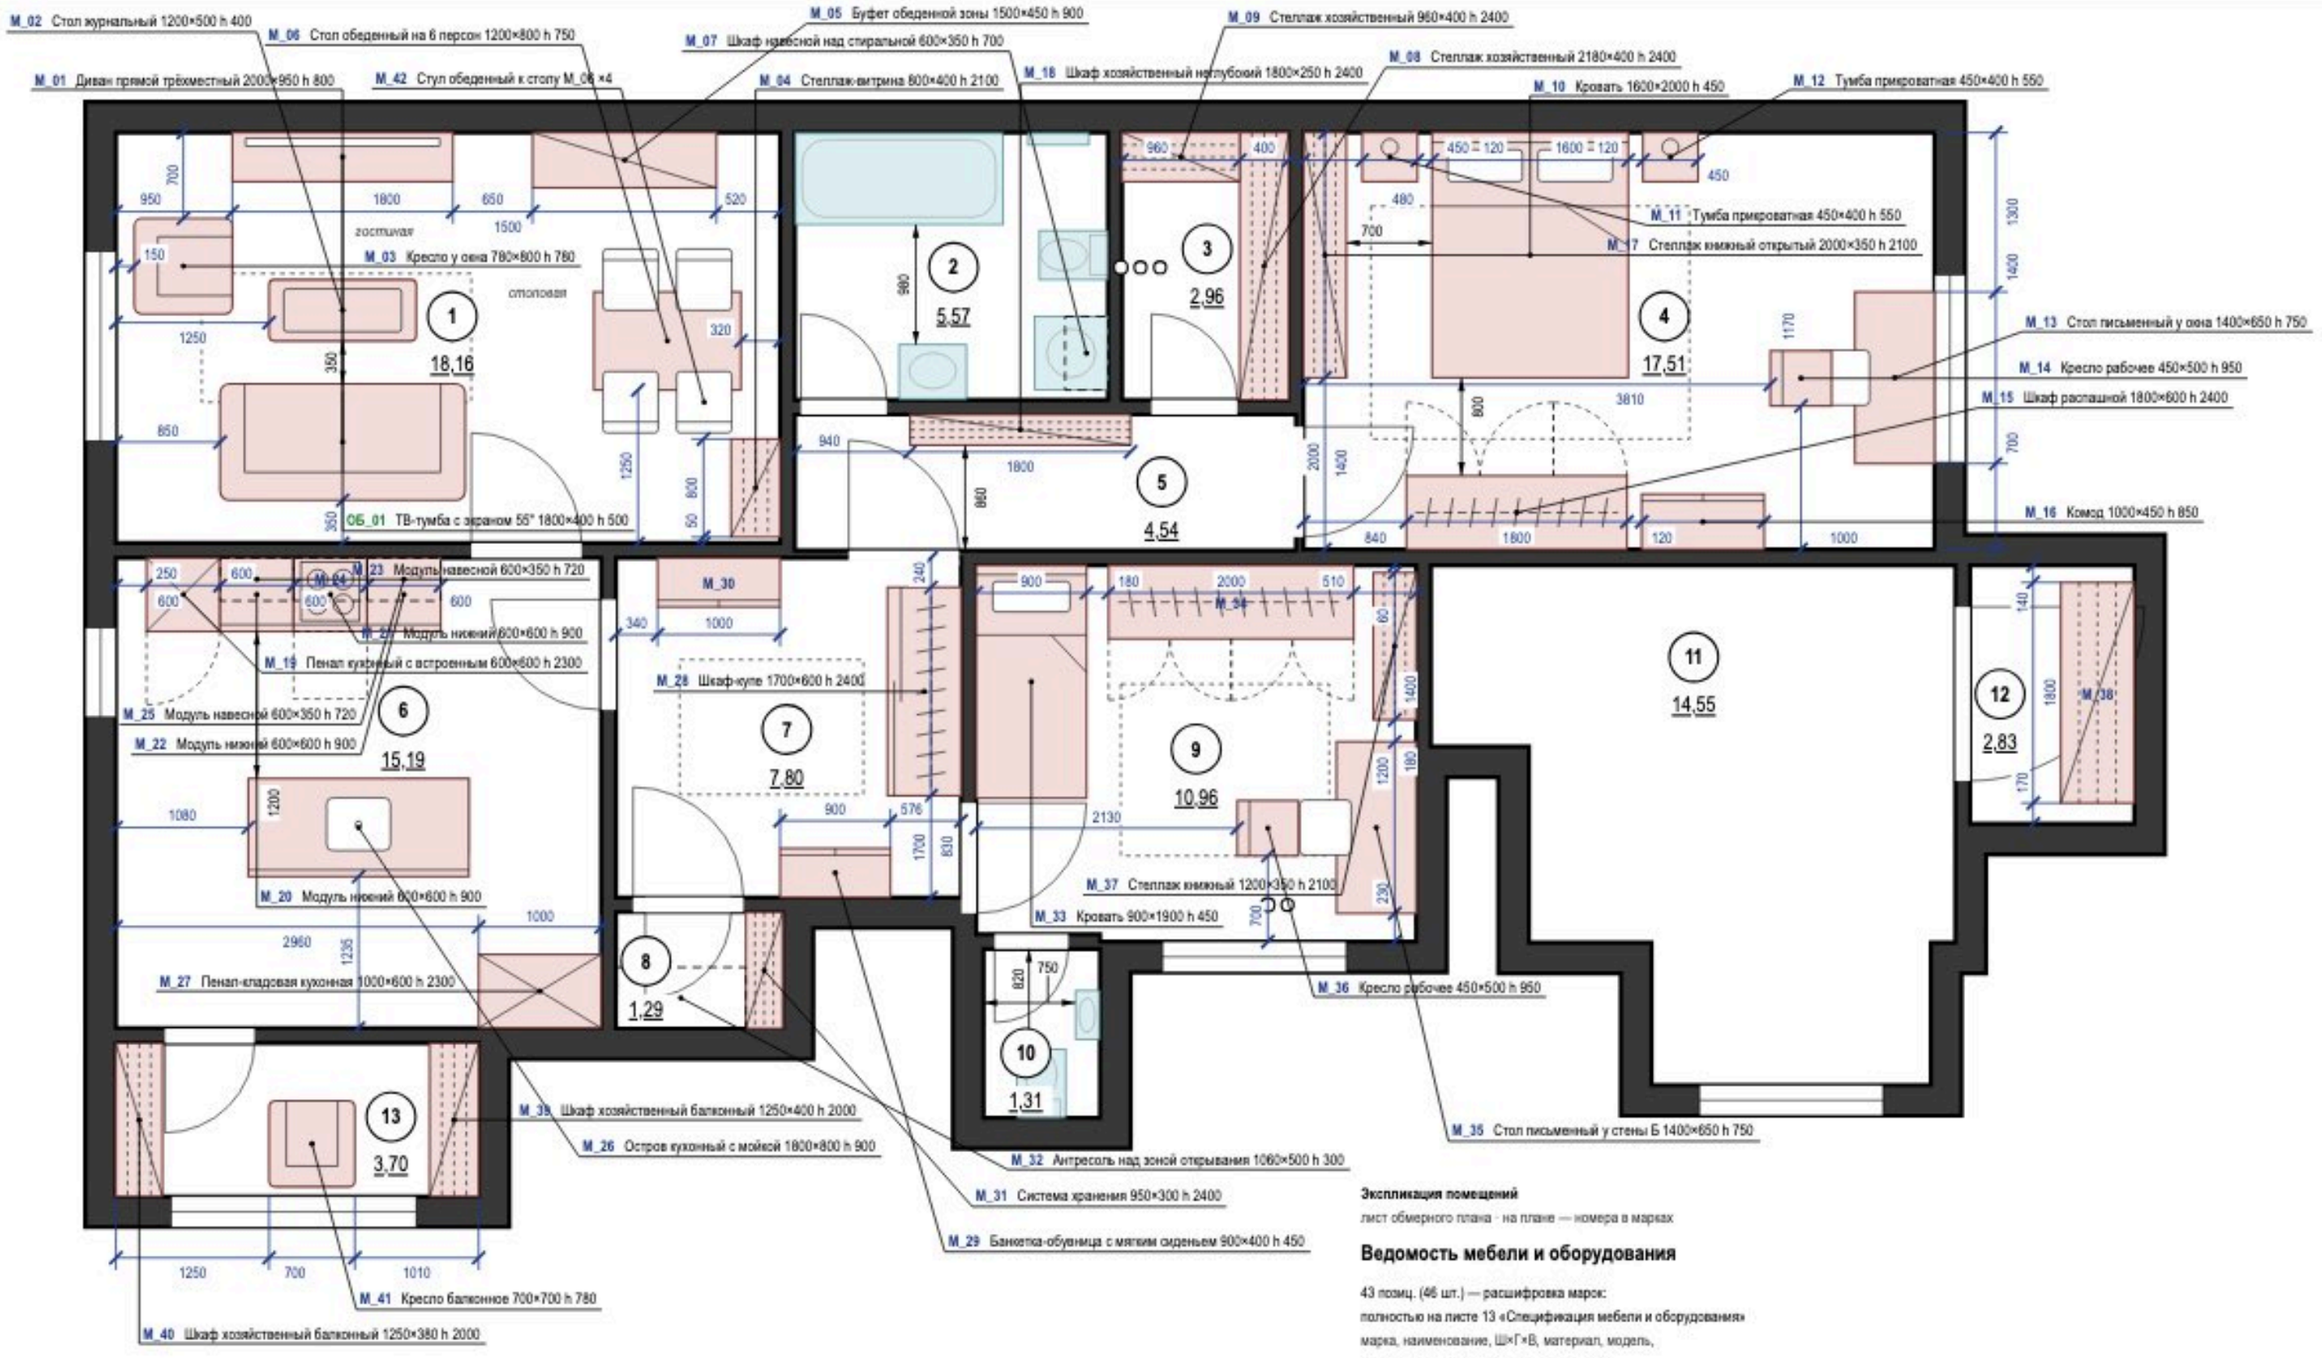

Экспликация помещений

лист обмерного плана · на плане — номера в марках

Ведомость мебели и оборудования

43 позиц. (46 шт.) — расшифровка марок:
полностью на листе 13 «Спецификация мебели и оборудования»
марка, наименование, Ш×Г×В, материал, модель,
допуск замены. Марки на плане — по ней.

Примечания

1. Размеры — в мм от чистовых поверхностей стен; размеры мебели уточнить после отделочных работ; общие указания — лист 2.
2. Отступ от стены, на плане не образмерен: M_41 — 80 мм.
3. Стулья обеденной группы (M_42 — 4 шт.) показаны в рабочем положении, задвинутыми под столешницу на 150 мм.

					Проект: Четырёхкомнатная квартира	
	Лист	№ док.	Подпись	Дата	План размещения мебели и оборудования	Стадия / Лист / Листов
Дизайнер	Кырпан А.С.			05.10.26		П / 12 / 111

выпуск 05.10.2026 № d0efc1af8a · стр. 12 из 111

Поз.	Наименование и техническая характеристика	Тип, марка, обозначение документа, опросного листа	Код продукции	Поставщик	Ед. измерения	Кол.	Масса 1 ед., кг	Примечание
	Мебель встроенная и корпусная (изготовление по чертежам мебельщика)							
M_08	Стеллаж хозяйственный, 6 полок; дерево — дуб натуральный; Ш×Г×В 2180×400×2400 мм			изготовление на заказ	шт.	1		пом. 3; крепление к стене
M_09	Стеллаж хозяйственный, 6 полок; дерево — дуб натуральный; Ш×Г×В 960×400×2400 мм			изготовление на заказ	шт.	1		пом. 3; крепление к стене
M_15	Шкаф распашной, 3 секции; дерево — дуб натуральный; Ш×Г×В 1800×600×2400 мм			изготовление на заказ	шт.	1		пом. 4; крепление к стене
M_18	Шкаф хозяйственный неглубокий; дерево — дуб натуральный; Ш×Г×В 1800×250×2400 мм			изготовление на заказ	шт.	1		пом. 5; крепление к стене
M_19	Пенал кухонный с встроенным холодильником; дерево — дуб натуральный, металл — чёрный матовый; Ш×Г×В 600×600×2300 мм			изготовление на заказ	шт.	1		пом. 6; крепление к стене
M_20	Модуль нижний, ящики; металл — чёрный матовый; Ш×Г×В 600×600×900 мм			изготовление на заказ	шт.	1		пом. 6
M_21	Модуль нижний: варочная панель и духовой шкаф; металл — чёрный матовый; Ш×Г×В 600×600×900 мм			изготовление на заказ	шт.	1		пом. 6
M_22	Модуль нижний, ящики и бутылочница; металл — чёрный матовый; Ш×Г×В 600×600×900 мм			изготовление на заказ	шт.	1		пом. 6
M_23	Модуль навесной, 2 секции; металл — чёрный матовый; Ш×Г×В 600×350×720 мм			изготовление на заказ	шт.	1		пом. 6
M_24	Вытяжка встраиваемая в шкаф; металл — чёрный матовый; Ш×Г×В 600×350×600 мм			изготовление на заказ	шт.	1		пом. 6
M_25	Модуль навесной, 2 секции; металл — чёрный матовый; Ш×Г×В 600×350×720 мм			изготовление на заказ	шт.	1		пом. 6
M_26	Остров кухонный с мойкой и посудомоечной машиной; дерево — дуб натуральный, металл — чёрный матовый; Ш×Г×В 1800×800×900 мм			изготовление на заказ	шт.	1		пом. 6
M_27	Пенал-кладовая кухонная; дерево — дуб натуральный, металл — чёрный матовый; Ш×Г×В 1000×600×2300 мм			изготовление на заказ	шт.	1		пом. 6; крепление к стене
M_28	Шкаф-купе, 3 двери; дерево — дуб натуральный, металл — чёрный матовый; Ш×Г×В 1700×600×2400 мм			изготовление на заказ	шт.	1		пом. 7; крепление к стене
M_31	Система хранения: штанга, полки, ящики; дерево — дуб натуральный; Ш×Г×В 950×300×2400 мм			изготовление на заказ	шт.	1		пом. 8; крепление к стене
M_32	Антресоль над зоной открывания двери; дерево — дуб натуральный; Ш×Г×В 1060×500×300 мм			изготовление на заказ	шт.	1		пом. 8; крепление к стене
M_34	Шкаф распашной, 4 секции; дерево — дуб натуральный; Ш×Г×В 2000×600×2400 мм			изготовление на заказ	шт.	1		пом. 9; крепление к стене
M_38	Система хранения торцевая: штанги, полки; дерево — дуб натуральный; Ш×Г×В 1800×600×2400 мм			изготовление на заказ	шт.	1		пом. 12; крепление к стене
M_39	Шкаф хозяйственный балконный; дерево — дуб натуральный; Ш×Г×В 1250×400×2000 мм			изготовление на заказ	шт.	1		пом. 13; крепление к стене
M_40	Шкаф хозяйственный балконный; дерево — дуб натуральный; Ш×Г×В 1250×380×2000 мм			изготовление на заказ	шт.	1		пом. 13; крепление к стене
	Мебель покупная							
M_01	Диван прямой трёхместный; обивка букле; Ш×Г×В 2000×950×800 мм	диван прямой, глубокая посадка, съёмные чехлы		аналог по характеристикам	шт.	1		пом. 1; допуск замены Ш 1900–2100, Г ≤ 1000
M_02	Стол журнальный; дерево — дуб натуральный; Ш×Г×В 1200×500×400 мм	стол журнальный прямоугольный		аналог по характеристикам	шт.	1		пом. 1; допуск замены Ш 1100–1300
M_03	Кресло у окна; обивка — ткань, цвет Tikkurila V486; Ш×Г×В 780×800×780 мм	кресло мягкое на деревянных ножках		аналог по характеристикам	шт.	1		пом. 1; допуск замены Ш 750–850, В ≤ 790 (не выше подоконника)
M_04	Стеллаж-витрина; дерево — дуб натуральный, металл — латунь; Ш×Г×В 800×400×2100 мм	стеллаж открытый, 5 полок		аналог по характеристикам	шт.	1		пом. 1; крепление к стене; допуск замены Ш 750–850
M_05	Буфет обеденной зоны; дерево — дуб натуральный, металл — латунь; Ш×Г×В 1500×450×900 мм	буфет 3-дверный		аналог по характеристикам	шт.	1		пом. 1; крепление к стене; допуск замены Ш 1400–1600, Г ≤ 470

Примечания

1. Позиции мебели совпадают с марками на плане расстановки; размеры Ш×Г×В — Ш вдоль стены, Г от стены.
2. Встроенная и корпусная мебель изготавливается по чертежам мебельщика после контрольного обмера; графы «Тип, марка» и «Код продукции» для неё не заполняются (ГОСТ 21.110-2013).
3. Покупные изделия — аналог по характеристикам: заменять только на изделия не больше указанного габарита и того же материала и цвета.
4. Материал и цвет, не указанные в данных изделия, приняты по концепции: тон дерева — по полу, обивка — по вторичному цвету палитры; образцы согласовать до заказа.
5. Масса 1 ед. для изделий до 25 кг не указывается. Техника — по монтажным схемам изготовителя; выводы — по листам ЭОМ и ВК.

					Проект: Четырёхкомнатная квартира			
	Лист	№ док.	Подпись	Дата	Спецификация мебели и оборудования	Стадия	Лист	Листов
Дизайнер	Кырпан А.С.			05.10.26		П	13	111

выпуск 05.10.2026 · d0efc1af8a · стр. 13 из 111

Поз.	Наименование и техническая характеристика	Тип, марка, обозначение документа, опросного листа	Код продукции	Поставщик	Ед. измерения	Кол.	Масса 1 ед., кг	Примечание
M_06	Стол обеденный на 6 персон; дерево — дуб натуральный; Ш×Г×В 1200×800×750 мм	стол обеденный прямоугольный, раскладной до 1800		аналог по характеристикам	шт.	1		пом. 1; допуск замены Ш 1200–1400 в сложенном виде, Г 800–900
M_42	Стул обеденный к столу M_06; обивка — ткань, цвет Tikkurila V486; каркас — дуб натуральный; Ш×Г×В 450×500×820 мм			аналог по характеристикам	шт.	4		пом. 1; замена ≤ габарита
ОБ_01	ТВ-тумба с экраном 55" дерево — дуб натуральный, металл — латунь; Ш×Г×В 1800×400×500 мм	тумба ТВ подвесная, 3 ящика		аналог по характеристикам	шт.	1		пом. 1; допуск замены Ш 1700–1900, Г ≤ 450
M_07	Шкаф навесной над стиральной машиной; дерево — дуб натуральный, металл — хром; Ш×Г×В 600×350×700 мм			аналог по характеристикам	шт.	1		пом. 2; крепление к стене; замена ≤ габарита
M_10	Кровать 1600×2000; мягкое изголовье, обивка — ткань, цвет Tikkurila V486; Ш×Г×В 1600×2000×450 мм	кровать с мягким изголовьем		аналог по характеристикам	шт.	1		пом. 4; допуск замены Ш 1600, Д 2000–2050
M_11, M_12	Тумба прикроватная; дерево — дуб натуральный; Ш×Г×В 450×400×550 мм	тумба прикроватная, 2 ящика		аналог по характеристикам	шт.	2		пом. 4; допуск замены Ш 400–500
M_13	Стол письменный у окна; дерево — дуб натуральный, металл — чёрный матовый; Ш×Г×В 1400×650×750 мм	стол письменный с тумбой		аналог по характеристикам	шт.	1		пом. 4; допуск замены Ш 1300–1500, Г 600–700
M_14, M_36	Кресло рабочее; металл — чёрный матовый; Ш×Г×В 450×500×950 мм	кресло рабочее на роликах		аналог по характеристикам	шт.	2		пом. 4, 9; допуск замены Ш 480–560
M_16	Комод, 4 ящика; дерево — дуб натуральный; Ш×Г×В 1000×450×850 мм	комод 4 ящика		аналог по характеристикам	шт.	1		пом. 4; крепление к стене; допуск замены Ш 950–1100
M_17	Стеллаж книжный открытый; дерево — дуб натуральный; Ш×Г×В 2000×350×2100 мм			аналог по характеристикам	шт.	1		пом. 4; крепление к стене; замена ≤ габарита
M_29	Банкетка-обувница с мягким сиденьем; дерево — дуб натуральный; Ш×Г×В 900×400×450 мм	банкетка-обувница		аналог по характеристикам	шт.	1		пом. 7; допуск замены Ш 800–950
M_30	Консоль прихожей, 3 ящика; дерево — дуб натуральный, металл — чёрный матовый; Ш×Г×В 1000×400×850 мм	консоль-комод		аналог по характеристикам	шт.	1		пом. 7; крепление к стене; допуск замены Ш 950–1100
M_33	Кровать 900×1900; мягкое изголовье, обивка — ткань, цвет Tikkurila V486; Ш×Г×В 900×1900×450 мм	кровать односпальная с мягким изголовьем		аналог по характеристикам	шт.	1		пом. 9; допуск замены Ш 900, Д 1900–1950
M_35	Стол письменный у стены Б, рядом с окном стены В: свет боковой; дерево — дуб натуральный, металл — чёрный матовый; Ш×Г×В 1400×650×750 мм	стол письменный с тумбой		аналог по характеристикам	шт.	1		пом. 9; допуск замены Ш 1300–1500, Г 600–700
M_37	Стеллаж книжный; дерево — дуб натуральный; Ш×Г×В 1200×350×2100 мм			аналог по характеристикам	шт.	1		пом. 9; крепление к стене; замена ≤ габарита
M_41	Кресло балконное; металл — чёрный матовый; Ш×Г×В 700×700×780 мм	кресло на металлическом каркасе		аналог по характеристикам	шт.	1		пом. 13; допуск замены Ш 650–750, В ≤ 850 (не выше подоконника)
	Техника встраиваемая и бытовая, светильники под розетки							
	Стиральная машина встраиваемая, у M_07			аналог по характеристикам	шт.	1		пом. 2; по схеме изготовителя
	Холодильник встраиваемый, в модуле M_19			аналог по характеристикам	шт.	1		пом. 6; по схеме изготовителя
	Духовой шкаф встраиваемый, в модуле M_21			аналог по характеристикам	шт.	1		пом. 6; по схеме изготовителя
	Варочная панель встраиваемая, электрическая, в модуле M_21			аналог по характеристикам	шт.	1		пом. 6; по схеме изготовителя
	Вытяжка встраиваемая, в модуле M_24			аналог по характеристикам	шт.	1		пом. 6; по схеме изготовителя
	Посудомоечная машина встраиваемая, в модуле M_26; ниша 600 мм			аналог по характеристикам	шт.	1		пом. 6; по схеме изготовителя

					Проект: Четырёхкомнатная квартира	
	Лист	№ док.	Подпись	Дата	Спецификация мебели и оборудования (продолжение)	Стадия: П; Лист: 14; Листов: 111
Дизайнер	Кырпан А.С.			05.10.26		

выпуск 05.10.2026 · d0efc1af8a · стр. 14 из 111

Поз.	Наименование и техническая характеристика	Тип, марка, обозначение документа, опросного листа	Код продукции	Поставщик	Ед. измерения	Кол.	Масса 1 ед., кг	Примечание
	Торшер, у поз. M_01; абажур — ткань или опаловое стекло; лампа 2700 K			аналог по характеристикам	шт.	1		пом. 1; розетка Р3 (ЭОМ)
	Текстиль							
T1	Портьеры-волна, два полотна; лён 100 %; цвет Tikkurila V486; карниз 2150 мм, высота 2690 мм, сборка 2			аналог по характеристикам	шт.	2		пом. 1
T2	Тюль-вуаль, одно полотно; полиэстер 100 %; цвет Tikkurila F497; карниз 2150 мм, высота 2690 мм, сборка 2,5			аналог по характеристикам	шт.	1		пом. 1
T3	Ковёр мягкой группы; шерсть 100 %; цвет NCS S 3005-Y20R; 2200×1050 мм			аналог по характеристикам	шт.	1		пом. 1; с подложкой
T4	Подушки декоративные на диван; лён 100 %; цвет Tikkurila H487			аналог по характеристикам	шт.	3		пом. 1
T5	Подушки декоративные на диван, акцент; хлопковый бархат 100 %; цвет Tikkurila L481			аналог по характеристикам	шт.	2		пом. 1
T6	Плед на диван; шерсть мериноса 100 %; цвет Tikkurila L481			аналог по характеристикам	шт.	1		пом. 1
T7	Раннер на обеденный стол; лён 100 %; цвет Tikkurila J484			аналог по характеристикам	шт.	1		пом. 1
T8	Портьеры стационарные, два полотна; лён 55 %, хлопок 45 %; цвет Tikkurila V484; карниз 2140 мм, высота 2690 мм, сборка 2			аналог по характеристикам	шт.	2		пом. 4
T9	Римская штора блэкаут: окно закрывает она, стол M_13 у окна не мешает; хлопок 100 %, подкладка полиэстер; цвет Tikkurila H487; карниз 1650 мм, высота 1900 мм			аналог по характеристикам	шт.	1		пом. 4
T10	Ковёр у кровати; шерсть 80 %, хлопок 20 %; цвет Tikkurila H487; 2600×1900 мм			аналог по характеристикам	шт.	1		пом. 4; с подложкой
T11	Подушки декоративные на кровать; лён 100 %; цвет Tikkurila H487			аналог по характеристикам	шт.	2		пом. 4
T12	Подушка декоративная, акцент; хлопковый бархат 100 %; цвет NCS S 5010-B10G			аналог по характеристикам	шт.	1		пом. 4
T13	Плед на кровать; хлопок 100 %; цвет NCS S 5010-B10G			аналог по характеристикам	шт.	1		пом. 4
T14	Рулонная штора кассетная, ткань димаут; полиэстер 100 %; цвет Tikkurila J484; карниз 890 мм, высота 1900 мм			аналог по характеристикам	шт.	1		пом. 6
T15	Ковёр прихожей, низкий ворс; шерсть 80 %, полиамид 20 %; цвет NCS S 3005-Y20R; 1500×1100 мм			аналог по характеристикам	шт.	1		пом. 7; с подложкой
T16	Портьеры стационарные, два полотна, до подоконника: радиатор под окном открыт; лён 55 %, хлопок 45 %; цвет Tikkurila V484; карниз 1800 мм, высота 1930 мм, сборка 2			аналог по характеристикам	шт.	2		пом. 9
T17	Римская штора блэкаут: закрывает проём целиком, радиатор под окном не задевает; хлопок 100 %, подкладка полиэстер; цвет Tikkurila H487; карниз 1620 мм, высота 1900 мм			аналог по характеристикам	шт.	1		пом. 9
T18	Ковёр игровой зоны; шерсть 100 %; цвет NCS S 3005-Y20R; 1700×1400 мм			аналог по характеристикам	шт.	1		пом. 9; с подложкой
T19	Подушки декоративные на кровать; лён 100 %; цвет Tikkurila H487			аналог по характеристикам	шт.	2		пом. 9
T20	Подушка декоративная, акцент; шерсть 60 %, полиэстер 40 %; цвет Farrow & Ball No. 47			аналог по характеристикам	шт.	1		пом. 9
T21	Плед на кровать; хлопок 100 %; цвет Farrow & Ball No. 47			аналог по характеристикам	шт.	1		пом. 9
T22	Рулонная штора кассетная, солнцезащитная; полиэстер 100 %; цвет Tikkurila V486; карниз 2140 мм, высота 1700 мм			аналог по характеристикам	шт.	1		пом. 13
T23	Плед на кресло M_41; шерсть 100 %; цвет Tikkurila V484			аналог по характеристикам	шт.	1		пом. 13
	Декор							
ДК1	Картина над диваном: крупная абстракция, холст, тонкая рама; 1400×900 мм; низ на 1000 мм от пола			аналог по характеристикам	шт.	1	6	пом. 1; крепление: планка на дюбелях, 4 точки
ДК2	Зеркало над буфетом, рама шпон дуба; 1000×800 мм; низ на 1100 мм от пола			аналог по характеристикам	шт.	1	12	пом. 1; крепление: анкер химический, 4 точки

					Проект: Четырёхкомнатная квартира	
	Лист	№ док.	Подпись	Дата	Спецификация мебели и оборудования (продолжение)	Стадия / Лист / Листов
Дизайнер	Кырпан А.С.			05.10.26		П / 15 / 111

выпуск 05.10.2026 № d0efc1af8a · стр. 15 из 111

Поз.	Наименование и техническая характеристика	Тип, марка, обозначение документа, опросного листа	Код продукции	Поставщик	Ед. измерения	Кол.	Масса 1 ед., кг	Примечание
ДК3	Фикус пировидный в кашпо Ø400; 450×450 мм			аналог по характеристикам	шт.	1		пом. 1
ДК4	Зеркало над раковиной C_03, влагостойкое; 600×800 мм; низ на 1100 мм от пола			аналог по характеристикам	шт.	1	5	пом. 2; крепление: зеркалодержатели, 4 точки
ДК5	Картина над изголовьем: графика, паспарту, рама; 1100×700 мм; низ на 1300 мм от пола			аналог по характеристикам	шт.	1	4	пом. 4; крепление: две петли на дюбелях
ДК6	Зеркало над комодом M_16; 700×900 мм; низ на 1050 мм от пола			аналог по характеристикам	шт.	1	8	пом. 4; крепление: анкер химический, 4 точки
ДК7	Хлорофитум хохлатый в напольном кашпо Ø380; 420×420 мм			аналог по характеристикам	шт.	1		пом. 4
ДК8	Часы настенные Ø400; 400×400 мм; центр на 1550 мм от пола			аналог по характеристикам	шт.	1	2	пом. 6; крепление: дюбель с крюком, 1 точка
ДК9	Хлорофитум хохлатый на подоконнике (отм. +0,800); 300×200 мм; низ на 800 мм от пола			аналог по характеристикам	шт.	1		пом. 6
ДК10	Зеркало над консолью M_30; 700×1000 мм; низ на 1050 мм от пола			аналог по характеристикам	шт.	1	9	пом. 7; крепление: анкер химический, 4 точки
ДК11	Замиокулькас в напольном кашпо Ø360; 400×400 мм			аналог по характеристикам	шт.	1		пом. 7
ДК12	Картина над изголовьем: графика, паспарту, рама; 600×800 мм; низ на 1200 мм от пола			аналог по характеристикам	шт.	1	3	пом. 9; крепление: две петли на дюбелях
ДК13	Постер в раме, левый (группа «постеры»); 400×500 мм; низ на 1250 мм от пола			аналог по характеристикам	шт.	1	2	пом. 9; крепление: петля на дюбеле
ДК14	Постер в раме, средний (группа «постеры»); 400×500 мм; низ на 1250 мм от пола			аналог по характеристикам	шт.	1	2	пом. 9; крепление: петля на дюбеле
ДК15	Постер в раме, правый (группа «постеры»); 400×500 мм; низ на 1250 мм от пола			аналог по характеристикам	шт.	1	2	пом. 9; крепление: петля на дюбеле
ДК16	Спатифиллум в напольном кашпо Ø360; 400×400 мм			аналог по характеристикам	шт.	1		пом. 9
ДК17	Зеркало над раковиной C_07, влагостойкое; 500×700 мм; низ на 1150 мм от пола			аналог по характеристикам	шт.	1	4	пом. 10; крепление: зеркалодержатели, 4 точки
ДК20	Картина: тёмная лиловая абстракция, холст, тонкая рама; 800×600 мм; низ на 1300 мм от пола			аналог по характеристикам	шт.	1	4	пом. 11; крепление: планка на дюбелях, 2 точки
ДК21	Ваза напольная, керамика матовая; 300×300 мм			аналог по характеристикам	шт.	1		пом. 11
ДК18	Зеркало ростовое 500×1600; 500×1600 мм; низ на 250 мм от пола			аналог по характеристикам	шт.	1	12	пом. 12; крепление: анкер химический, 4 точки + опора снизу
ДК19	Лавр благородный в напольном кашпо Ø380; 400×400 мм			аналог по характеристикам	шт.	1		пом. 13

					Проект: Четырёхкомнатная квартира	
	Лист	№ док.	Подпись	Дата		
Дизайнер	Кырпан А.С.			05.10.26	Спецификация мебели и оборудования (продолжение)	Стадия: П; Лист: 16; Листов: 111

выпуск 05.10.2026 · d0efc1af8a · стр. 16 из 111

Ведомость изделий

Марка	Наименование	Пом.	Ш×Г×В, мм	Корпус	Фасад	Кромка, мм скр./вид.	Кол.
M_07	Система хранения	2	600×350×700	ЛДСП 16	без фасадов; ящики — МДФ 18, эмаль матовая	0,4 / 2	1
M_08	Система хранения	3	2180×400×2400	ЛДСП 16	без фасадов; ящики — МДФ 18, эмаль матовая	0,4 / 2	1
M_09	Система хранения	3	960×400×2400	ЛДСП 16	без фасадов; ящики — МДФ 18, эмаль матовая	0,4 / 2	1
M_15	Шкаф распашной	4	1800×600×2400	ЛДСП 16	МДФ 18, эмаль матовая	0,4 / 2	1
M_17	Система хранения	4	2000×350×2100	ЛДСП 16	без фасадов; ящики — МДФ 18, эмаль матовая	0,4 / 2	1
M_18	Система хранения	5	1800×250×2400	ЛДСП 16	МДФ 18, эмаль матовая	0,4 / 2	1
M_28	Шкаф-купе	7	1700×600×2400	ЛДСП 16	рифлёные панели МДФ в алюминиевом профиле	0,4 / 2	1
M_31	Система хранения	8	950×300×2400	ЛДСП 16	без фасадов; ящики — МДФ 18, эмаль матовая	0,4 / 2	1
M_32	Система хранения	8	1060×500×300	ЛДСП 16	без фасадов; ящики — МДФ 18, эмаль матовая	0,4 / 2	1
M_34	Шкаф распашной	9	2000×600×2400	ЛДСП 16	МДФ 18, эмаль матовая	0,4 / 2	1
M_38	Система хранения	12	1800×600×2400	ЛДСП 16	без фасадов; ящики — МДФ 18, эмаль матовая	0,4 / 2	1
M_39	Система хранения	13	1250×400×2000	ЛДСП 16	без фасадов; ящики — МДФ 18, эмаль матовая	0,4 / 2	1
M_40	Система хранения	13	1250×380×2000	ЛДСП 16	без фасадов; ящики — МДФ 18, эмаль матовая	0,4 / 2	1
M_19	Пенал: холодильник встр.	6	600×600×2300	ЛДСП 16	МДФ 18, эмаль матовая	0,4 / 2	1
M_20	Модуль нижний: ящики	6	600×600×900	ЛДСП 16	МДФ 18, эмаль матовая	0,4 / 2	1
M_23	Модуль навесной: полки	6	600×350×720	ЛДСП 16	МДФ 18, эмаль матовая	0,4 / 2	1
M_21	Модуль нижний: духовой шкаф, варочная	6	600×600×900	ЛДСП 16	МДФ 18, эмаль матовая	0,4 / 2	1
M_24	Модуль навесной: полки	6	600×350×600	ЛДСП 16	МДФ 18, эмаль матовая	0,4 / 2	1
M_22	Модуль нижний: ящики	6	600×600×900	ЛДСП 16	МДФ 18, эмаль матовая	0,4 / 2	1
M_25	Модуль навесной: полки	6	600×350×720	ЛДСП 16	МДФ 18, эмаль матовая	0,4 / 2	1
M_27	Пенал: полки	6	1000×600×2300	ЛДСП 16	МДФ 18, эмаль матовая	0,4 / 2	1

Ведомость встраиваемой техники

Поз.	Прибор	Ниша, вырез, мм	Вентиляция	Питание	Схема
M_19	Холодильник встраиваемый, ниша 1780	ниша 1780 × 560 × 550	решётка в цоколе, канал за корпусом, выход сверху	розетка над нишей или в соседнем модуле	по модели
M_21	Духовой шкаф встраиваемый, 60 см	ниша 560 × 595, глубина ≥ 550	зазор за шкафом, вырез в задней стенке	вывод кабеля под шкафом	по модели
M_21	Варочная панель индукционная, 60 см	вырез в столешнице 560 × 490		вывод кабеля под модулем	по модели
M_21	Вытяжка настенная, 60 см	низ ≥ 650 над панелью	воздуховод к вентканалу, короб до потолка	вывод кабеля в коробе	по модели

Ведомость фурнитуры

№	Фурнитура	Тип, размер	Изделия	Кол.
1	Полкодержатель с фиксацией	ø5 мм	M_07, M_08, M_09, M_15, M_17, M_18, M_28, M_31, M_32, M_34, M_38, M_39, M_40, M_19, M_23, M_24, M_25, M_27	344
2	Штанга выдвижная торцевая	L по глубине	M_07, M_08, M_09, M_17, M_32, M_39, M_40	11
3	Анкер по основанию стены	по таблице крепежа	M_07, M_08, M_09, M_15, M_17, M_18, M_28, M_31, M_32, M_34, M_38, M_39, M_40, M_23, M_24, M_25	96
4	Уголок крепления к стене от опрокидывания	стальной	M_07, M_08, M_09, M_15, M_17, M_18, M_28, M_31, M_32, M_34, M_38, M_39, M_40, M_19, M_27	30
5	Опора регулируемая с цоколем на клипсах	ход 20 мм	M_08, M_09, M_15, M_17, M_18, M_28, M_31, M_34, M_38, M_39, M_40	80
6	Петля накладная 110° с доводчиком	чашка 35 мм	M_15, M_18, M_34, M_19, M_23, M_24, M_25, M_27	96
7	Штанга овальная 30×15, L = 876	+ 2 держателя	M_15	1
8	Система дверей купе: профиль, направляющие, ролики	на 2 двери	M_28	1
9	Ручка-профиль вертикальная	в цвет профиля	M_28	2
10	Штанга овальная 30×15, L = 826	+ 2 держателя	M_28	1
11	Полка для обуви выдвижная наклонная	ширина 826	M_28	3
12	Штанга овальная 30×15, L = 976	+ 2 держателя	M_34	1
13	Штанга овальная 30×15, L = 579	+ 2 держателя	M_38	3
14	Ручка-профиль	латунь матовая	M_19, M_20, M_23, M_21, M_24, M_22, M_25, M_27	18
15	Опора кухонная регулируемая 100–120 мм	+ клипса цоколя	M_19, M_20, M_21, M_22, M_27	22
16	Направляющие полного выдвижения с доводчиком NL 500	пара	M_20, M_21, M_22	7
17	Навес регулируемый для навесного шкафа	пара на секцию	M_23, M_24, M_25	3
18	Шина монтажная	L = 540	M_23, M_24, M_25	3


Примечания

1. Модели техники выбирает заказчик до изготовления мебели; ниши, вырезы и вентиляция — по монтажной схеме выбранной модели (условие гарантии), её номер вносится в ведомость.
2. Количество фурнитуры — по чертежам изделий; запас крепежа 5 %. Аналоги — по характеристикам (доводчик, нагрузка, ход).
3. Цвет корпусов, фасадов и профилей — по колерной карте проекта.


					Проект: Четырёхкомнатная квартира			
	Лист	№ док.	Подпись	Дата	Ведомости изделий, техники и фурнитуры	Стадия	Лист	Листов
Дизайнер	Кырпан А.С.			05.10.26		П	17	111

выпуск 05.10.2026 · d0efc1af8a · стр. 17 из 111


Фрагмент 1. Ванная комната (пом. 2)

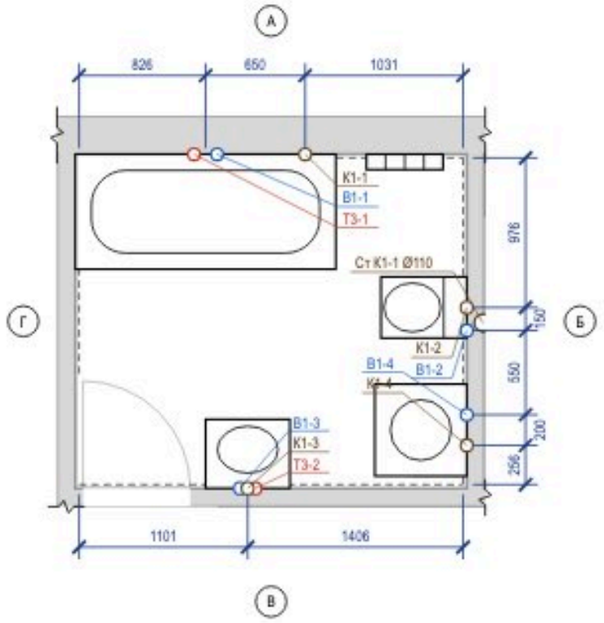

Фрагмент 2. Кухня (пом. 6)

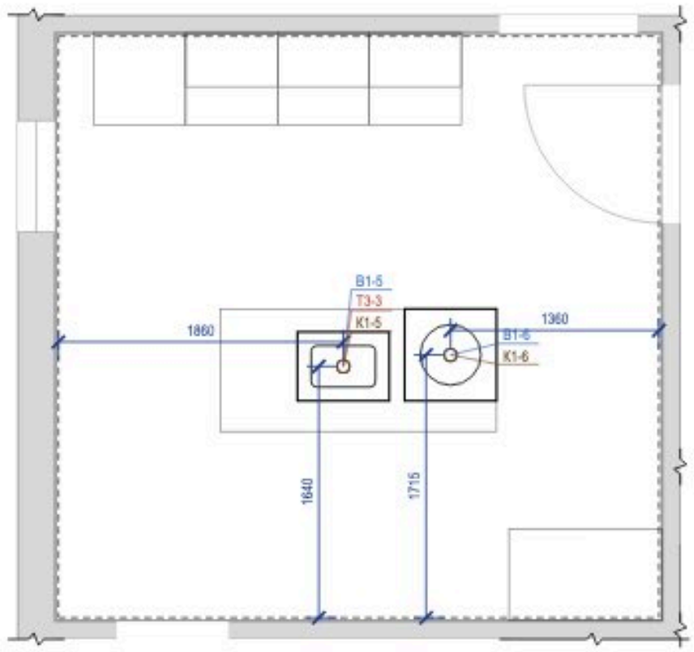

Фрагмент 3. Санузел (пом. 10)

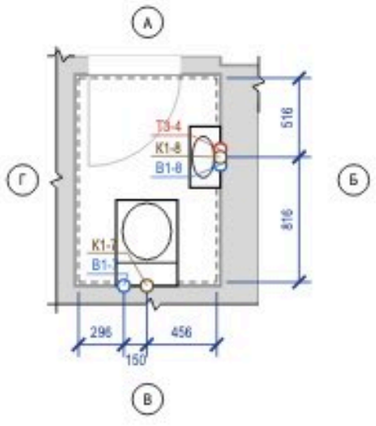

Ведомость привязок выводов

Код	Прибор	Ø	H, мм	Привязка от чист. стен, мм	Прим.
В1-1	С_01 ванна	½"	800	ст. А: 901 от Г	межос. 150
Т3-1	С_01 ванна	½"	800	ст. А: 751 от Г	межос. 150
К1-1	С_01 ванна	Ø50	60	ст. А: 1031 от Б	
В1-2	С_02 унитаз подвесной	½"	250	ст. Б: 1026 от В	в раме инсталляции
К1-2	С_02 унитаз подвесной	Ø110	220	ст. Б: 976 от А	
В1-3	С_03 умывальник	½"	550	ст. В: 1051 от Г	межос. 100
Т3-2	С_03 умывальник	½"	550	ст. В: 1151 от Г	межос. 100
К1-3	С_03 умывальник	Ø40	450	ст. В: 1101 от Г	
В1-4	ОБ_02 стиральная машина	½"	700	ст. Б: 456 от В	кран машины
К1-4	ОБ_02 стиральная машина	Ø40	700	ст. Б: 256 от В	
В1-5	С_05 мойка кухонная	½"	600	1860 от Г; 1640 от В	межос. 100
Т3-3	С_05 мойка кухонная	½"	600	1860 от Г; 1640 от В	межос. 100
К1-5	С_05 мойка кухонная	Ø50	400	1860 от Г; 1640 от В	
В1-6	ОБ_03 посудомоечная машина	½"	550	1360 от Б; 1715 от В	кран ПММ
К1-6	ОБ_03 посудомоечная машина	Ø50	550	1360 от Б; 1715 от В	
В1-7	С_06 унитаз подвесной	½"	250	ст. В: 296 от Г	в раме инсталляции
К1-7	С_06 унитаз подвесной	Ø110	220	ст. В: 446 от Г	
В1-8	С_07 умывальник	½"	550	ст. Б: 566 от А	межос. 100
Т3-4	С_07 умывальник	½"	550	ст. Б: 466 от А	межос. 100
К1-8	С_07 умывальник	Ø40	450	ст. Б: 516 от А	

Условные обозначения

- вывод В1 (код — в ведомости привязок)
- вывод Т3 (код — в ведомости привязок)
- вывод К1 (код — в ведомости привязок)
- сантехприбор по расстановке (габарит модели)
- чистовая поверхность стены (от неё привязки)
- стояк «Ст К1-N / Ст В1-N» (ГОСТ 21.601), Ø мм
- стояк Т3 не на обмере — принят в шахте рядом со Ст В1, сверить
- линия обрыва (граница фрагмента)
- А — обозначение стены А–Г (как на развёртках)

Примечания


1. Привязки выводов даны от чистовых поверхностей стен (облицовка на сторону: ванная комната — 24 мм (штукатурка 10 + клей 5 + плитка 9); кухня — 20 мм (по данным); санузел — 24 мм (штукатурка 10 + клей 5 + плитка 9)); эти же грани — на развёртках и в раскладке плитки. Высоты — от чистого пола помещения.
2. До черновой разводки сверить по паспорту выбранного прибора (смеситель, инсталляция, сифон).
3. Горячая вода (Т3) — слева от холодной (В1), если смотреть на прибор. Допуск установки выводов: ±5 мм в группе, ±20 мм у отдельно стоящих.
4. Расчёт систем водоснабжения и канализации и подбор оборудования выполняет проектная организация; лист задаёт места и высоты выводов.
5. Ст Т3-2 на обмере не показаны: приняты рядом с Ст В1-2 (в МКД стоят группой); положение сверить на объекте до разметки.
6. Штриховая линия чистовой грани стены прерывается на длине полотна открытой двери, лежащего вдоль грани (линии не должны сливаться при печати); положение грани — по размерам, а не по штрихе.

					Проект: Четырёхкомнатная квартира
	Лист	№ док.	Подпись	Дата	План выводов сантехники
Дизайнер	Кырпан А.С.			05.10.26	


Стадия	Лист	Листов
П	18	111

выпуск 05.10.2026 № d0efc1af8a · стр. 18 из 111


План квартиры (М 1:400)

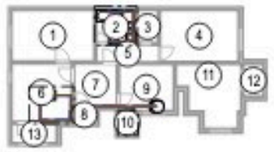


Фр. 1. Ванная комната (М 1:40)

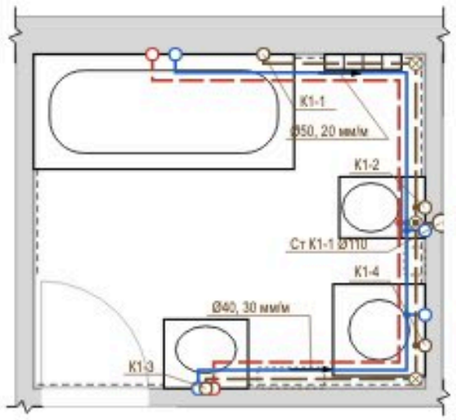

Фр. 2. Кухня (М 1:40)

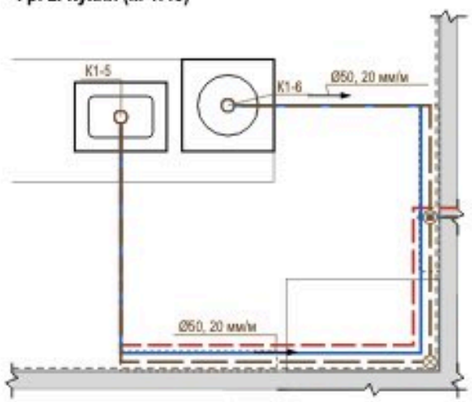

Фр. 3. Санузел (М 1:40)

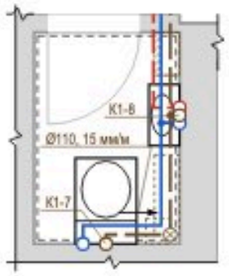

Условные обозначения


- В1 — водопровод хозяйственно-питьевой (ХВС), PP-R Ø20
- Т3 — горячее водоснабжение, подача (ГВС), PP-R Ø20
- К1 — канализация бытовая
- направление уклона К1 / пола: Ø, мм на 1 м
- ⊗ ревизия (прочистка) К1 — доступ сохранить
- • тройник (ответвление к прибору)
- короб К1 над чистым полом (ГКЛВ под плитку)
- ○ вывод В1 (код — в ведомости привязок)
- ○ вывод Т3 (код — в ведомости привязок)
- ○ вывод К1 (код — в ведомости привязок)
- сантехприбор по расстановке (габарит модели)
- ○ стояк «Ст К1-N / Ст В1-N» (ГОСТ 21.601), Ø мм
- ◌ стояк Т3 не на обмере — принят в шахте рядом со Ст В1, сверить
- ∿ линия обрыва (граница фрагмента)
- граница фрагмента на плане (Фр. N)

Профиль выпусков К1 (до врезки в стояк)

Выпуск	Прибор	Ø	L, м	i, мм/м	Δh, мм	Прокладка, мм
К1-7	С_06 унитаз подвесной	Ø110	3,60	15	54	короб 200×140
К1-2	С_02 унитаз подвесной	Ø110	0,35	20	7	над полом за приборами
К1-5	С_05 мойка кухонная	Ø50	10,10	20	202	короб 290×110
К1-6	ОБ_03 посудомоечная машина	Ø50	7,60	20	152	короб 240×110
К1-1	С_01 ванна	Ø50	2,30	20	46	в полу, стяжка ≥ 151
К1-3	С_03 умывальник	Ø40	2,65	30	80	короб 150×110
К1-8	С_07 умывальник	Ø40	2,50	30	75	короб 150×110
К1-4	ОБ_02 стиральная машина	Ø40	1,05	30	32	в полу, стяжка ≥ 127

Короб h×b: h — от чистого пола, b — от чистовой стены. Стяжка 155 мм — лист полов.

Узел ввода В1, Т3 (схема, без масштаба)

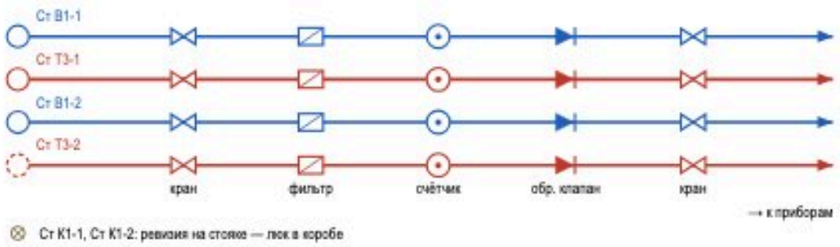

⊗ Ст К1-1, Ст К1-2: ревизия на стояке — люк в коробе

Примечания

1. Трассы принципиальные, построены от стояков вдоль стен помещений; фактическое положение фиксируется исполнительной схемой с привязками (фото с рулеткой) до закрытия.
2. Уклон К1 не менее 1/d и не более 150 мм/м (СП 30.13330.2020, п. 19.1), приняты практические уклоны; поворот — двумя отводами 45°, ревизия после поворота, доступ сохранить. Стояк К1 в коробе — звукоизоляция стояка в коробе, без жёсткого контакта короба с трубой.
3. Решение по К1: стяжка 155 мм не укрывает трубы (нужно Ø + Δh + 45 мм) — выпуски идут над чистым полом вдоль стен К1-2 — за приборами и в раме инсталляции; К1-7, К1-5, К1-6, К1-3, К1-8 — в коробе ГКЛВ под плитку (размеры в профиле). Короба — на развёртках; отметку низа врезки в стояк замерить до черновых работ.
4. На каждом вводе В1 и Т3 — кран шаровой, фильтр, счётчик, обратный клапан; доступ через люк не меньше 300×400. Водопровод — в штробе стен или в коробах; трубы испытать давлением до закрытия (акт скрытых работ).
5. Расчёт систем, диаметры магистралей и подбор оборудования выполняет проектная организация; врезка и перенос стояков — по согласованию с управляющей организацией. Арматуру и привязки сверить по паспортам приборов.
6. Ст Т3-2 на обмере не показана: приняты рядом с Ст В1-2; положение сверить на объекте до разводки.
7. Штриховая линия чистовой грани стены прерывается на длине полотна открытой двери, лежащего вдоль грани (линии не должны сливаться при печати); положение грани — по размерам, а не по штрихе.

					Проект: Четырёхкомнатная квартира
	Лист	№ док.	Подпись	Дата	Схема разводки водопровода и канализации
Дизайнер	Кырпан А.С.			05.10.26	

Стадия	Лист	Листов
П	19	111

выпуск 05.10.2026 · d0efc1af8a · стр. 19 из 111


Поз.	Наименование и техническая характеристика	Тип, марка, обозначение документа	Код продукции	Поставщик	Ед. изм.	Кол.	Масса 1 ед., кг	Примечание
	Санитарные приборы							
1	Ванна акриловая 1700×750 мм, с каркасом, экраном и отверстием слив-перелив	аналог		выбор заказчика	шт	1	35	С_01
2	Унитаз подвесной безободковый, с сиденьем микролифт, крепёж и звукоизолирующая прокладка	аналог		выбор заказчика	шт	2		С_02, С_06
3	Инсталляция для подвесного унитаза: рама высотой 1120 мм, бачок, клавиша смыва (ось клавиши 1050 мм от чистого пола)	аналог		выбор заказчика	шт	2		С_02, С_06; короб ГКЛВ
4	Умывальник подвесной 550×450 мм, с отверстием под смеситель и переливом	аналог		выбор заказчика	шт	1		С_03
5	Умывальник подвесной 400×200 мм, с отверстием под смеситель и переливом	аналог		выбор заказчика	шт	1		С_07
6	Мойка кухонная врезная 600×450 мм, с переливом	аналог		с кухонной мебелью	шт	1		С_05
7	Полотенцесушитель электрический, IP44, с терморегулятором	аналог		выбор заказчика	шт	1		С_04
	Смесители, сифоны и арматура приборов							
8	Смеситель для ванны настенный однорычажный, межосевое 150 мм, с душевым набором (лейка, шланг, держатель)	аналог		выбор заказчика	шт	1		С_01
9	Смеситель для умывальника однорычажный, с донным клапаном	аналог		выбор заказчика	шт	2		С_03, С_07
10	Смеситель кухонный однорычажный, высокий излив	аналог		выбор заказчика	шт	1		С_05
11	Обвязка ванны слив-перелив Ø40/50 с сифоном	аналог		выбор заказчика	шт	1		С_01
12	Сифон для умывальника бутылочный Ø32/40–50, с гофрой к выпуску	аналог		выбор заказчика	шт	2		С_03, С_07
13	Сифон для мойки с отводом для ПММ Ø40/50	аналог		выбор заказчика	шт	1		С_05
14	Сифон для стиральной машины встраиваемый в стену Ø50, с обратным клапаном	аналог		выбор заказчика	шт	1		ОБ_02
15	Кран угловой ½"×½" с гибкой подводкой 40 см (умывальники, мойка)	аналог		выбор заказчика	шт	6		по 2 на прибор
16	Кран шаровой угловой ½"×¾" для подключения стиральной и посудомоечной машины	аналог		выбор заказчика	шт	2		ОБ_02, ОБ_03
	Трубопроводы							
17	Труба полипропиленовая PP-R PN20 Ø20×3,4 (В1)	ГОСТ 32415-2013		выбор заказчика	м	27	0,17	20,1 + 4,3 + 10 %
18	Труба PP-R, армированная стекловолокном, PN20 Ø20×2,8 (Т3)	ГОСТ 32415-2013		выбор заказчика	м	21,5	0,15	16,7 + 2,5 + 10 %
19	Труба канализационная ПП Ø40 (К1)	ГОСТ 32414-2013		выбор заказчика	м	5		2,6 + 1,6 + 10 %
20	Труба канализационная ПП Ø50 (К1)	ГОСТ 32414-2013		выбор заказчика	м	15,5		12,7 + 1,0 + 10 %
21	Труба канализационная ПП Ø110 (К1)	ГОСТ 32414-2013		выбор заказчика	м	5		3,9 + 0,4 + 10 %
	Фасонные части и выводы							
22	Отвод канализационный ПП 45° Ø40	ГОСТ 32414-2013		выбор заказчика	шт	4		2 шт. на поворот
23	Отвод канализационный ПП 45° Ø50	ГОСТ 32414-2013		выбор заказчика	шт	12		2 шт. на поворот
24	Отвод канализационный ПП 45° Ø110	ГОСТ 32414-2013		выбор заказчика	шт	10		2 шт. на поворот
25	Тройник канализационный ПП 45° (врезки ветвей)	ГОСТ 32414-2013		выбор заказчика	шт	7		
26	Ревизия канализационная ПП (после поворота трассы)	ГОСТ 32414-2013		выбор заказчика	шт	7		доступ сохранить
27	Фитинги PP-R Ø20: тройники, угольники 90° (ветви и повороты В1, Т3)	ГОСТ 32415-2013		выбор заказчика	шт	30		
28	Водорозетка PP-R Ø20×½" настенная, с креплением	ГОСТ 32415-2013		выбор заказчика	шт	12		коды — лист выводов
	Узлы ввода, люки, короба							
29	Кран шаровой латунный Ду15 PN16 (отключение ввода)	аналог		выбор заказчика	шт	4		Ст В1-1, Ст Т3-1, Ст В1-2, Ст Т3-2
30	Фильтр сетчатый косой Ду15	аналог		выбор заказчика	шт	4		
31	Счётчик воды крыльчатый Ду15 (ХВ, ГВ), с поверкой	аналог		выбор заказчика	шт	4		пломба УК
32	Клапан обратный Ду15	аналог		выбор заказчика	шт	4		
33	Люк ревизионный накимной под плитку 300×400 мм	аналог		выбор заказчика	шт	4		к стоякам и арматуре
34	Звукоизоляция стояка К1 в коробе: рулонный звукоизоляционный материал ≥ 10 мм, обмотка стояка на высоту этажа	аналог		выбор заказчика	м	5,4		Ст К1-1, Ст К1-2
35	Короб К1 над полом: профиль ПНПС, ГКЛВ 12,5 мм под плитку	аналог		выбор заказчика	м	6,8		сечение — лист разводки

Примечания

1. Форма 1 ГОСТ 21.110-2013, ширины граф изменены по п. 4.1. «Аналог» — аналог по характеристикам: модели внести до черновых работ, привязки выводов сверить по паспортам.
2. Бытовая техника не входит (показана арматура подключения), мойка — в комплекте кухни. Длины труб — трасса листа разводки + подъёмы + 10 %.
3. Стояк К1 в коробе — звукоизоляция стояка в коробе без жёсткого контакта короба с трубой.
4. Расчёт систем водоснабжения и канализации, диаметры магистралей и подбор оборудования выполняет проектная организация.

					Проект: Четырёхкомнатная квартира			
	Лист	№ док.	Подпись	Дата	Спецификация сантехнического оборудования	Стадия	Лист	Листов
Дизайнер	Кырпан А.С.			05.10.26		П	20	111

выпуск 05.10.2026 · d0efc1af8a · стр. 20 из 111

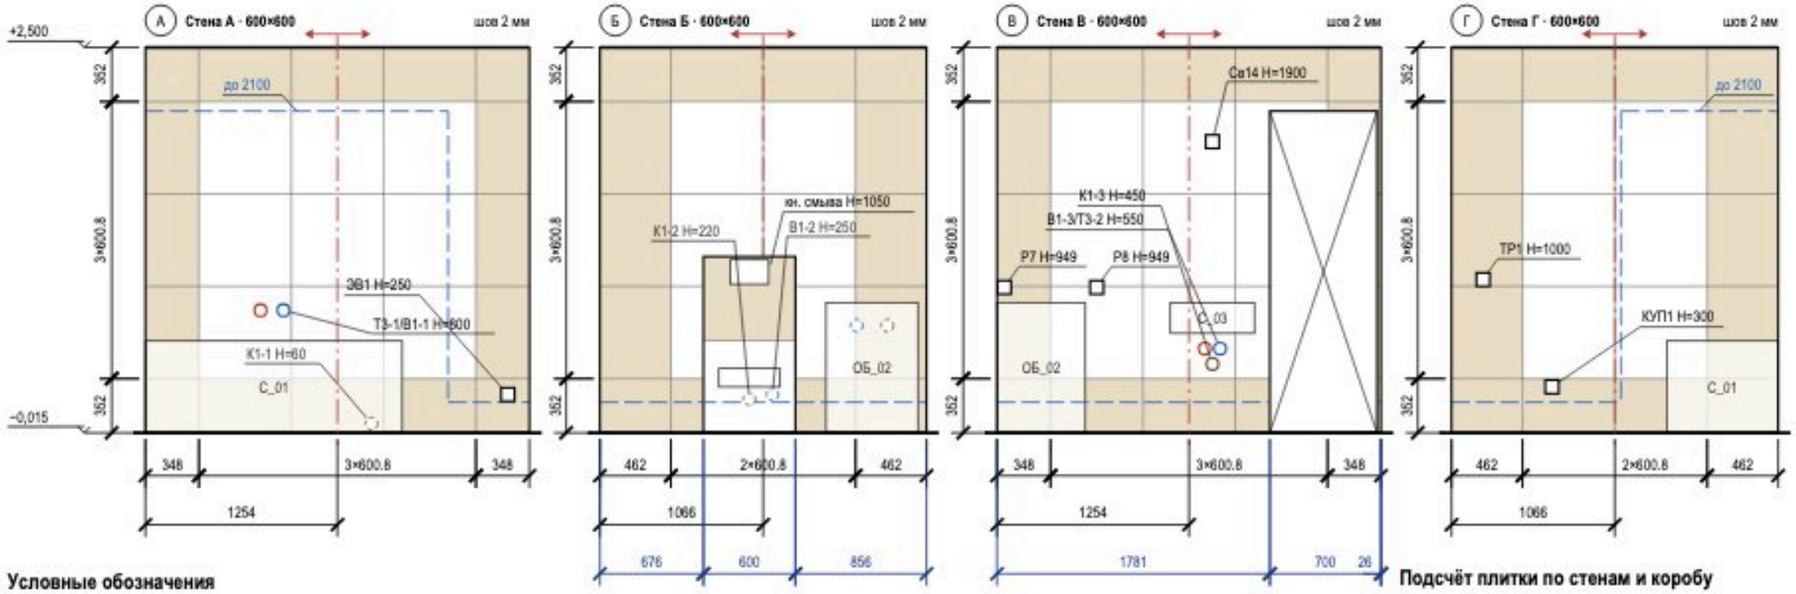

Условные обозначения

- плитка целая; тонкая линия — шов
- плитка с подрезкой (размер — на цепочке)
- ось старта; стрелки — направление укладки
- верх гидроизоляции: 200 от ЧП, в мокрой зоне — «до …»
- проём — не облицовывается
- сантехприбор: габарит, высота по практике
- короб инсталляции, в нём кнопка смыва 250×160
- вывод В1 (код — в ведомости привязок)
- вывод Т3 (код — в ведомости привязок)
- вывод К1 (код — в ведомости привязок)
- вывод за прибором / в коробе (не на сетке)
- электроточка: марка и Н — по листам ЭОМ
- отметка уровня, м: ±0,000 — чистый пол жилых помещений
- низ потолка; серая полоса — стена без плитки
- (А) обозначение стены А–Г (как на развёртках)

Примечания

1. Вид изнутри, стены по часовой стрелке А → Г. Высоты — от чистого пола (−0,015), отметки — от ±0,000. Раскладка от чистовых размеров (штукатурка 10 + клей 5 + плитка 9 мм), подрезки чистые; старт — от оси стены, ряды от середины (две подрезки).
2. Облицовка до потолка (+2,500).
3. Точки из таблицы сдвигов переносятся до черновой разводки: смеситель — по оси пары В1 + Т3; вывод на оси прибора — вместе с прибором, иначе старт раскладки — на ось прибора.
4. За приборами и в коробе (К1-1, В1-2, К1-2, В1-4, К1-4) — штриховым кольцом.
5. Гидроизоляция: 200 мм от ЧП по периметру; над ванной — до 2100 и 300 мм за борт (СП 29.13330.2011, п. 7.2 — на высоту замачивания); углы — лентой; акт скрытых работ, пролив.
6. Короб 600×1150×230: лицо 600 мм от оси кнопки смыва, боковины, полка; углы — запил 45° или профиль; за коробом плитку не кладут.
7. Наружные углы: ст. Б: 2 — запил 45°; ст. В: 2 — профиль.
8. Люк: Л1 (ст. Б, 600×600, нажимной) — кромки дверцы по швам сетки.

Подсчёт плитки по стенам и коробу


Поверхность	L × H, мм	S, м²	Целых	Подр.	С запасом	Подрезки: край / верх, мм
стена А	2507 × 2515	6,43	9	16	28	348 / 348; 352
стена Б	2132 × 2515	4,79	2	18	22	462 / 462; 352
короб (ст. Б)	600×1150×230	1,36	1	6	8	лицо 600; бок. 230
стена В	2507 × 2515	4,96	6	19	28	348 / 348; 352
стена Г	2132 × 2515	5,48	6	14	22	462 / 462; 352
Итого		**23,01**	**24**	**73**	**108**	

Сдвиг точек под раскладку

Точка (ВК, ЭОМ)	Стена	Проект: от угла / Н	Под раскладку: от угла / Н	Сдвиг, мм
Т3-1/В1-1	А	826 / 800	952 / 655	+126 на шов; Н −145
ЗВ1	А	2368 / 250	2459 / 353	+93 в центр плитки; Н +103
В1-3/Т3-2	В	1406 / 550	1555 / 655	+149 на шов; Н +105
К1-3	В	1406 / 450	1253 / 353	−153 в центр плитки; Н −97
Св14	В	1406 / 1900	1555 / 1860	+149 на шов; Н −40
ТР1	Г	206 / 1000	162 / 956	−44 в центр плитки; Н −44
КУП1	Г	656 / 300	765 / 353	+109 в центр плитки; Н +53

	Лист	№ док.	Подпись	Дата	Проект: Четырёхкомнатная квартира			
Дизайнер	Кырпан А.С.			05.10.26	Раскладка плитки. Ванная комната. Развёртки стен	Стадия	Лист	Листов
						П	21	111

выпуск 05.10.2026 · d0efc1af8a · стр. 21 из 111

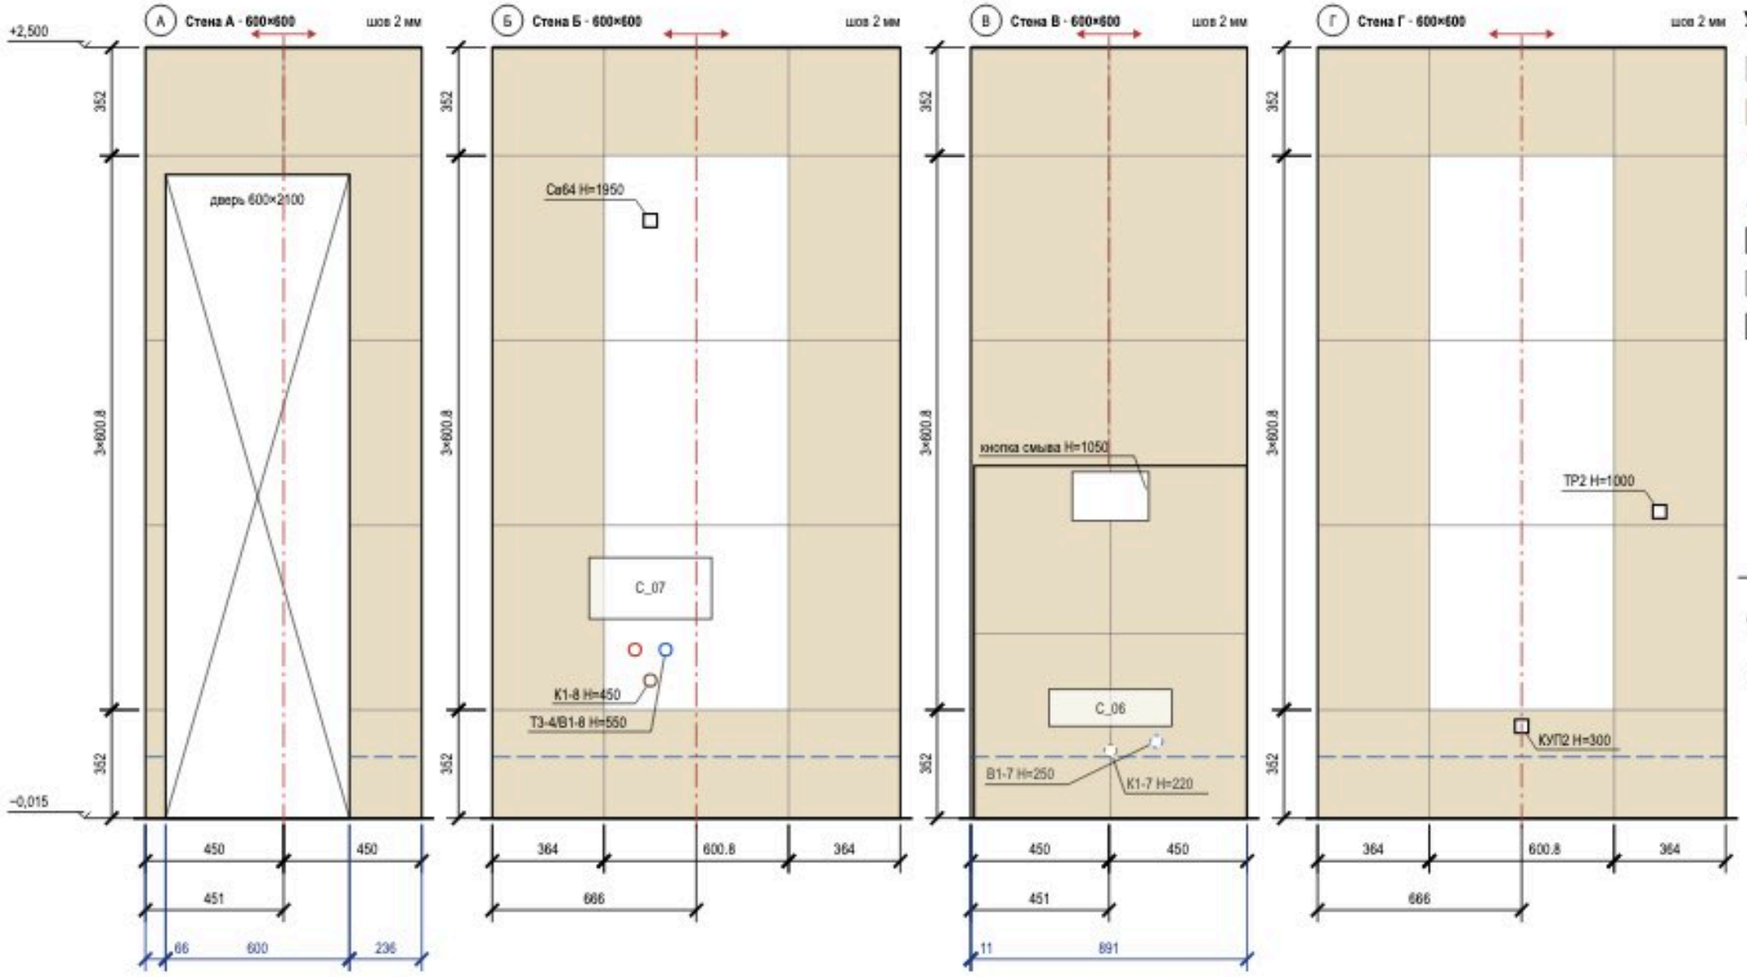

Условные обозначения

- плитка целая; тонкая линия — шов
- плитка с подрезкой (размер — на цепочке)
- ось старта; стрелки — направление укладки
- верх гидроизоляции: 200 от ЧП, в мокрой зоне — «до …»
- проём — не облицовывается
- сантехприбор: габарит, высота по практике
- короб инсталляции, в нём кнопка смыва 250×160
- вывод В1 (код — в ведомости привязок)
- вывод Т3 (код — в ведомости привязок)
- вывод К1 (код — в ведомости привязок)
- вывод за прибором / в коробе (не на сетке)
- электроточка: марка и H — по листам ЭОМ
- отметка уровня, м: ±0,000 — чистый пол жилых помещений
- низ потолка; серая полоса — стена без плитки
- (А) обозначение стены А–Г (как на развёртках)

Подсчёт плитки по стенам и коробу

Поверхность	L × H, мм	S, м²	Целых	Подр.	С запасом	Подрезки: край / верх, мм
стена А	902 × 2515	1,13	0	10	11	450 / 450; 352
стена Б	1332 × 2515	3,47	3	12	17	364 / 364; 352
стена В	902 × 2515	1,37	0	10	11	450 / 450; 352
короб (ст. В)	890×1150×230	1,76	0	10	11	лицо 444 / 444; бок. 230
стена Г	1332 × 2515	3,47	3	12	17	364 / 364; 352
Итого		**11,19**	**6**	**54**	**67**	

Сдвиг точек под раскладку

Точка (ВК, ЭОМ)	Стена	Проект: от угла / H	Под раскладку: от угла / H	Сдвиг, мм
Т3-4/В1-8	Б	516 / 550	666 / 655	+150 в центр плитки; H +105
К1-8	Б	516 / 450	666 / 353	+150 в центр плитки; H −97
Св64	Б	516 / 1950	666 / 1860	+150 в центр плитки; H −90
КУП2	Г	666 / 300	666 / 353	H +53
ТР2	Г	1116 / 1000	1269 / 956	+153 в центр плитки; H −44

Примечания

1. Вид изнутри, стены по часовой стрелке А → Г. Высоты — от чистого пола (−0,015), отметки — от ±0,000. Раскладка от чистовых размеров (штукатурка 10 + клей 5 + плитка 9 мм), подрезки чистые; старт — от оси стены, ряды от середины (две подрезки).
2. Облицовка до потолка (+2,500).
3. Точки из таблицы сдвигов переносятся до черновой разводки: смеситель — по оси пары В1 + Т3; вывод на оси прибора — вместе с прибором, иначе старт раскладки на ось прибора.
4. За приборами и в коробе (В1-7, К1-7) — штриховым кольцом.
5. Гидроизоляция: 200 мм от ЧП по периметру; углы — лентой; акт скрытых работ, пролив.
6. Короб 890×1150×230: лицо 444 / 444 мм от оси кнопки смыва, боковины, полка; углы — запил 45° или профиль; за коробом плитку не кладут.
7. Между коробом и углом полоса 11 мм — довести короб до угла.
8. Наружные углы: ст. А: 2 — профиль.


					Проект: Четырёхкомнатная квартира
	Лист	№ док.	Подпись	Дата	Раскладка плитки. Санузел. Развёртки стен
Дизайнер	Кырпан А.С.			05.10.26	

Стадия	Лист	Листов
П	22	111

выпуск 05.10.2026 · d0efc1af8a · стр. 22 из 111

Примечания

1. Размеры проёмов и привязки — в миллиметрах от чистых граней стен до отделки; привязка — от угла того помещения, со стороны которого стоит размер. Размер в ведомости — ширина × высота проёма от чистого пола 0,000.
2. Марки в кружках — типы заполнения проёмов (ГОСТ 21.501-2018, п. 5.3.2); одна марка — один типоразмер; количество сверено с планом.
3. Открывание: Л — петли слева, П — справа, если смотреть со стороны, куда открывается полотно (на себя).
4. Дверные блоки обычного монтажа (Д-1…Д-5) заказывать после чистовой стяжки и штукатурки, проёмы перемерить; монтажный зазор коробки 10–15 мм на сторону, откос от угла помещения до коробки — не менее 50 мм.
5. Размеры проёмов и привязки сняты со скана плана заказчика и на объекте не замерены (обмерный план — лист 3).
6. Экспликация помещений — лист 3; в марках помещений — номер и площадь, м².
7. Привязка проёма к углу помещения меньше 1 мм на листе, размер на плане не показан: Д-2 — 50 мм; Д-1 — 100 мм; Д-3 — 90 мм.

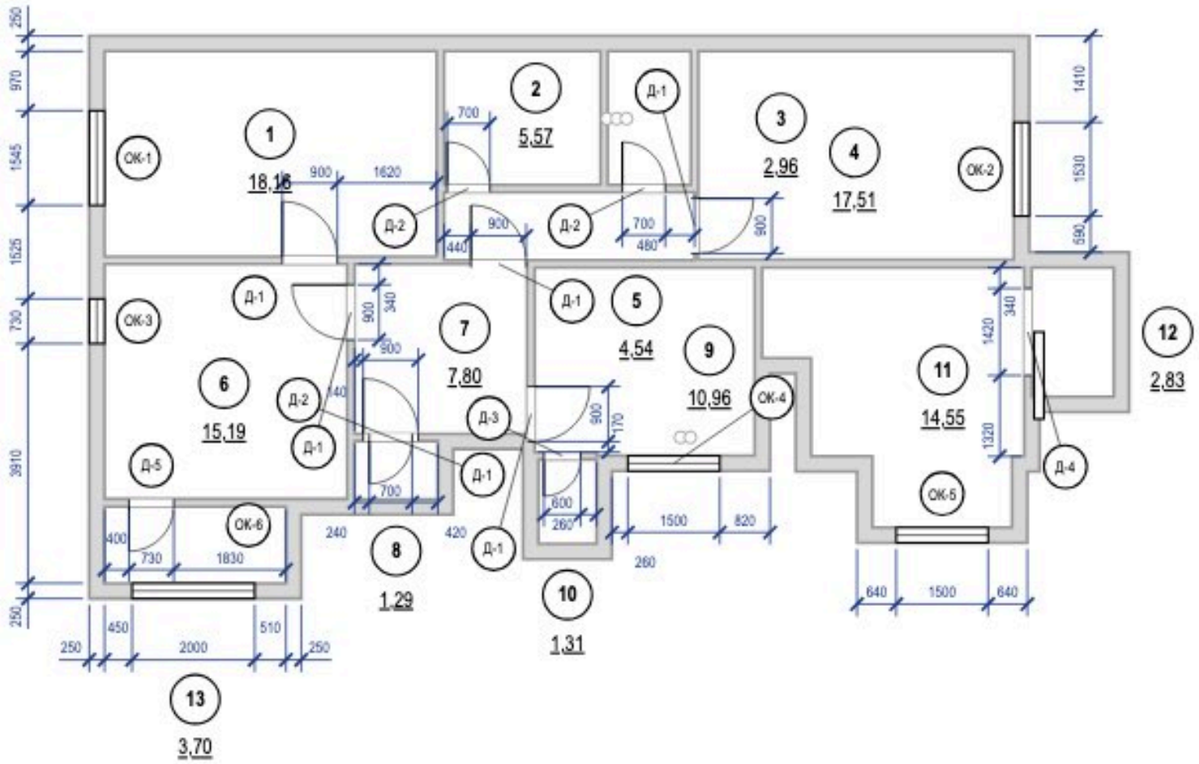

Ведомость заполнения проёмов

Марка	Наименование, обозначение	Проём ш×в, мм	Кол.	Откр.	Отделка полотна	Фурнитура	Прим.
Д-1	Блок дверной внутренний, ГОСТ 475-2016	900×2100	6	П, П, П, Л, П, П		петли, ручка с защёлкой	6/п
Д-2	Блок дверной внутренний, ГОСТ 475-2016	700×2100	3	П, П, Л		петли, ручка с защёлкой, фиксатор WC	пом. 2; порог 15
Д-3	Блок дверной внутренний, ГОСТ 475-2016	600×2100	1	Л		петли, ручка с защёлкой, фиксатор WC	порог 15
Д-4	Дверь раздвижная, ГОСТ 475-2016	1420×2100	1			раздвижная система, ручки-купе	пом. 12; 6/п
Д-5	Блок дверной внутренний, ГОСТ 475-2016	730×2100	1	Л		петли, ручка с защёлкой	порог 30
ОК-1	Блок оконный, ГОСТ 23166-2021	1545×1600	1				низ 800
ОК-2	Блок оконный, ГОСТ 23166-2021	1530×1600	1				низ 800
ОК-3	Блок оконный, ГОСТ 23166-2021	730×1600	1				низ 800
ОК-4	Блок оконный, ГОСТ 23166-2021	1500×1600	1				пом. 9; низ 800
ОК-5	Блок оконный, ГОСТ 23166-2021	1500×1600	1				пом. 11; низ 900
ОК-6	Блок оконный, ГОСТ 23166-2021	2000×1700	1				низ 900

					Проект: Четырёхкомнатная квартира			
	Лист	№ док.	Подпись	Дата	План размещения дверей	Стадия	Лист	Листов
Дизайнер	Кырпан А.С.			05.10.26		П	23	111

выпуск 05.10.2026 № d0efc1af8a · стр. 23 из 111



Ведомость потолков

Пом.	Марка	Конструкция	Низ	S, м²	Q
1	ПТ1	ГКЛ П113, короб LED	+2,500	2,37	Q3
1	ПТ2	ГКЛ П113	+2,600	15,29	Q3
1	НШ1	ниша под шторы 150×100	+2,700	0,50	
2	ПТ3	ГКЛВ П113	+2,500	5,57	Q3
3	ПТ2	ГКЛ П113	+2,600	2,96	Q3
4	ПТ2	ГКЛ П113	+2,600	17,00	Q3
4	НШ1	ниша под шторы 150×100	+2,700	0,51	
5	ПТ2	ГКЛ П113	+2,600	4,54	Q3
6	ПТ2	ГКЛ П113	+2,600	14,61	Q3
6	НШ1	ниша под шторы 150×100	+2,700	0,58	
7	ПТ2	ГКЛ П113	+2,600	7,80	Q3
8	ПТ2	ГКЛ П113	+2,600	1,29	Q3
9	ПТ2	ГКЛ П113	+2,600	10,48	Q3
9	НШ1	ниша под шторы 150×100	+2,700	0,48	
10	ПТ3	ГКЛВ П113	+2,500	1,31	Q3
11	ПТ2	ГКЛ П113	+2,600	14,21	Q3
11	НШ1	ниша под шторы 150×100	+2,700	0,34	
12	ПТ2	ГКЛ П113	+2,600	2,83	Q3
13	ПТ3	ГКЛВ П113	+2,500	3,26	Q3
13	НШ2	ниша под шторы 150×100	+2,600	0,44	
		Итого		**106,37**	

Ведомость вырезов и закладных в потолке

Марка	Устройство	Кол.	Пом.
	Светильник встраиваемый (марки — план освещения)	56	1, 2, 3, 4, 5, 6, 7, 8, 9, 10, 11, 12, 13
	Светильник подвесной (марки — план освещения)	1	1
ИП1, ИП2, ИП6, ИП7	Извещатель дымовой	4	1, 4, 9, 11
ИП3…ИП5	Извещатель тепловой	3	5, 6, 7
АР1, АР2	Точка доступа Wi-Fi, PoE	2	7, 11
ВР1, ВР3	Решётка вытяжная (вентилятор)	2	2, 10
	Люк ревизии 500×400, 400×300, 300×300	4	1, 3, 9, 11

Примечания


1. За отметку ±0,000 принят уровень чистого пола сухих помещений (готовое покрытие), а не существующего пола; пол пом. 2, 10, 13 — −0,015, −0,030; верх плиты перекрытия −0,170 — расчётный по пирогу пола, не замерен; существующий пол снимается до плиты, его отметка не замерена. Отметки в прямоугольниках — низ потолка; низ плиты перекрытия +2,700, +2,600. Марка потолка — одна конструкция и отметка на весь альбом.
2. Потолки ГКЛ — каркасная система П113: подвесы через 1000, несущие профили через 500, основные через 1200 мм; листы — поперёк несущих профилей. В помещениях 2, 10, 13 — ГКЛВ на оцинкованном каркасе.
3. LED-лента в алюминиевом профиле посередине карниза короба шириной 450 мм (узел 1, лист 25); длина по плану: пом. 1 — 5,4 м (в плане освещения 5); пом. 11 — 5,4 м.
4. Ниши под шторы 150×100 мм — на всю длину стены с окном; карниз — на закладной до обшивки (узел 2, лист 25).
5. Примыкание к стенам: теневой шов 15 мм, техзазор 3 мм — пом. 1, 11, по стенам, выровненным штукатуркой (узел 1); пом. 2, 3, 4, 5, 6, 7, 8, 9, 10, 12, 13 — разделительная лента.
6. Светильники и потолочные устройства — подложка с планов освещения, слаботочных систем и вентиляции (положение — по ним); вырезы и закладные — по ведомости на листе, до обшивки; отверстия не совмещать с профилями, глубина корпуса светильника до 70 мм.
7. Разрезы 1–1, 2–2 и узлы — на листе 25; высоты мебели и дверных блоков сверены с низом потолка в разрезах.
8. Шпаклевание ГКЛ и условия приёмки — Q3: рассеянный дневной свет, осмотр с 2 м; боковой свет не оценивается.
9. Люки ревизии 500×400, 400×300, 300×300 мм — по центру блоков питания LED (ревизия, ревизия, блок питания LED БП1, блок питания LED БП1; координаты — план освещения).

					Проект: Четырёхкомнатная квартира
	Лист	№ док.	Подпись	Дата	План потолков
Дизайнер	Кырпан А.С.			05.10.26	Стадия: П; Лист: 24; Листов: 111

выпуск 05.10.2026 · d0efc1af8a · стр. 24 из 111


Разрез 1–1 (М 1:40)

Пом. 1 Зал; линия разреза — план потолков, лист 24

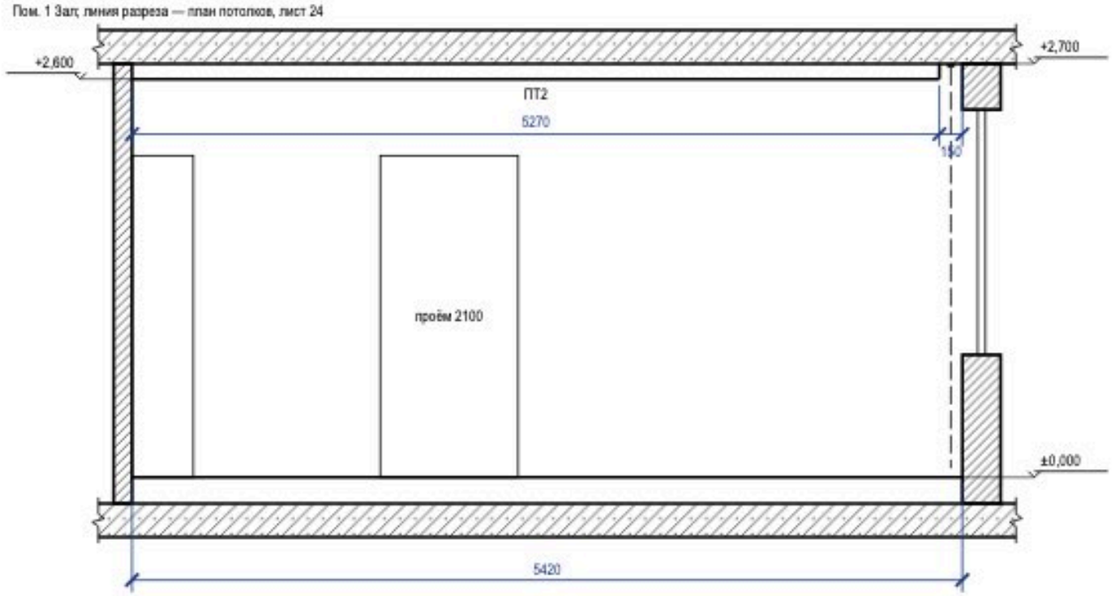


Разрез 2–2 (М 1:40)

Пом. 4 Детская 1; линия разреза — план потолков, лист 24

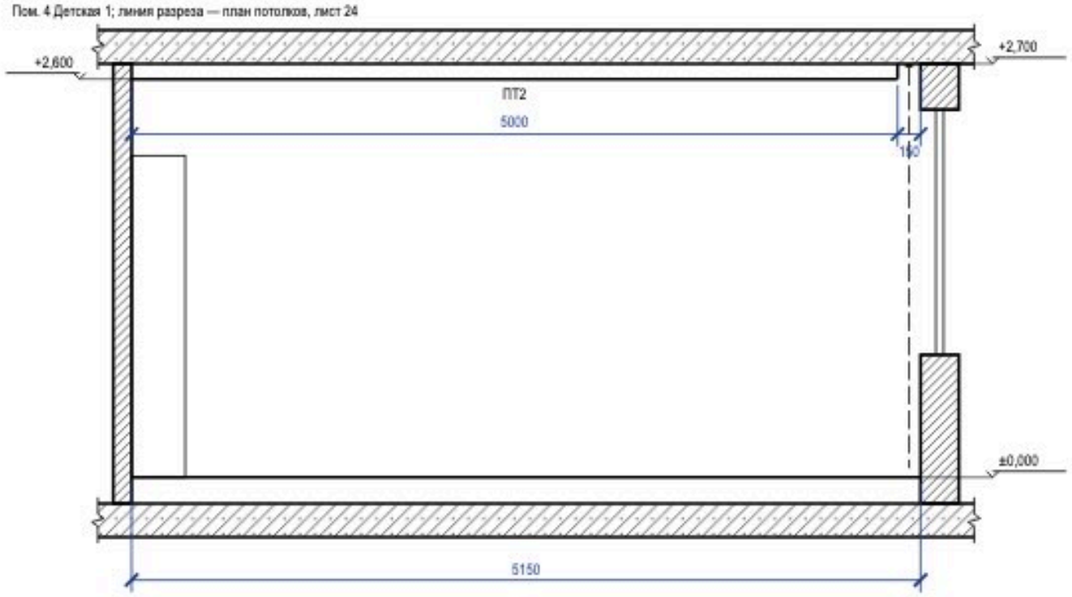

1 Короб с LED-подсветкой, теневой шов (М 1:10)


Пом. 1, 11; карниз 150×100, щель под свет 60 мм

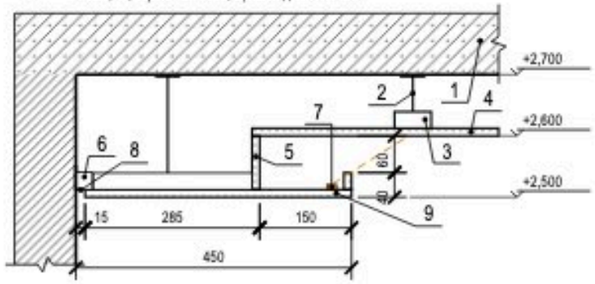

1 — плита перекрытия
2 — подвес прямой, шаг 1000 мм
3 — ПП 60×27: несущие через 500, основные через 1200 мм
4 — ГКЛ 12,5 по П113 — верхний уровень
5 — задняя стенка и бортик карниза — ГКЛ 12,5
6 — ПН 28×27 по периметру, к стене через 500 мм
7 — LED-лента в алюминиевом профиле
8 — теневой профиль: шов 15 мм, зазор 3 мм
9 — низ короба — ГКЛ 12,5 по ПП 60×27

2 Ниша под шторы (М 1:10)

Пом. 1, 4, 6, 9, 11, 13; без подсветки; закладные под карниз — до обшивки

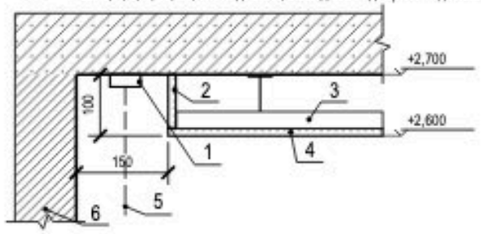

1 — карниз (шина), высота с верхом портьеры 80 мм
2 — стенка ниши — ГКЛ 12,5
3 — ПП 60×27 — каркас короба
4 — низ короба нижнего уровня — ГКЛ 12,5
5 — портьера
6 — стена с окном

Условные обозначения

- плита перекрытия в сечении
- стена в сечении
- потолок ГКЛ в сечении; под линией — марка потолка (план потолков)
- мебель и дверные проёмы за секущей плоскостью; число — марка и верх от чистого пола, мм
- портьера в нише под шторы


Примечания

1. Разрезы — по линиям 1–1, 2–2 на плане потолков (лист 24). Отметки — от ±0,000 чистого пола, м; размеры — мм.
2. Высоты мебели и дверных блоков за секущей плоскостью сверены с низом потолка над ними: верх ниже низа короба и поля.
3. ГКЛ 12,5 мм по каркасу П113; перепад уровней и бортик карниза — ГКЛ по ПП 60×27 (узел 1). Ниша под шторы — на всю длину стены с окном, карниз на закладной до обшивки (узел 2).
4. Толщины плит перекрытия и пирога пола показаны условно.

					Проект: Четырёхкомнатная квартира
	Лист	№ док.	Подпись	Дата	Разрезы и узлы потолков
Дизайнер	Кырпан А.С.			05.10.26	

Стадия	Лист	Листов
П	25	111

выпуск 05.10.2026 · d0efc1af8a · стр. 25 из 111

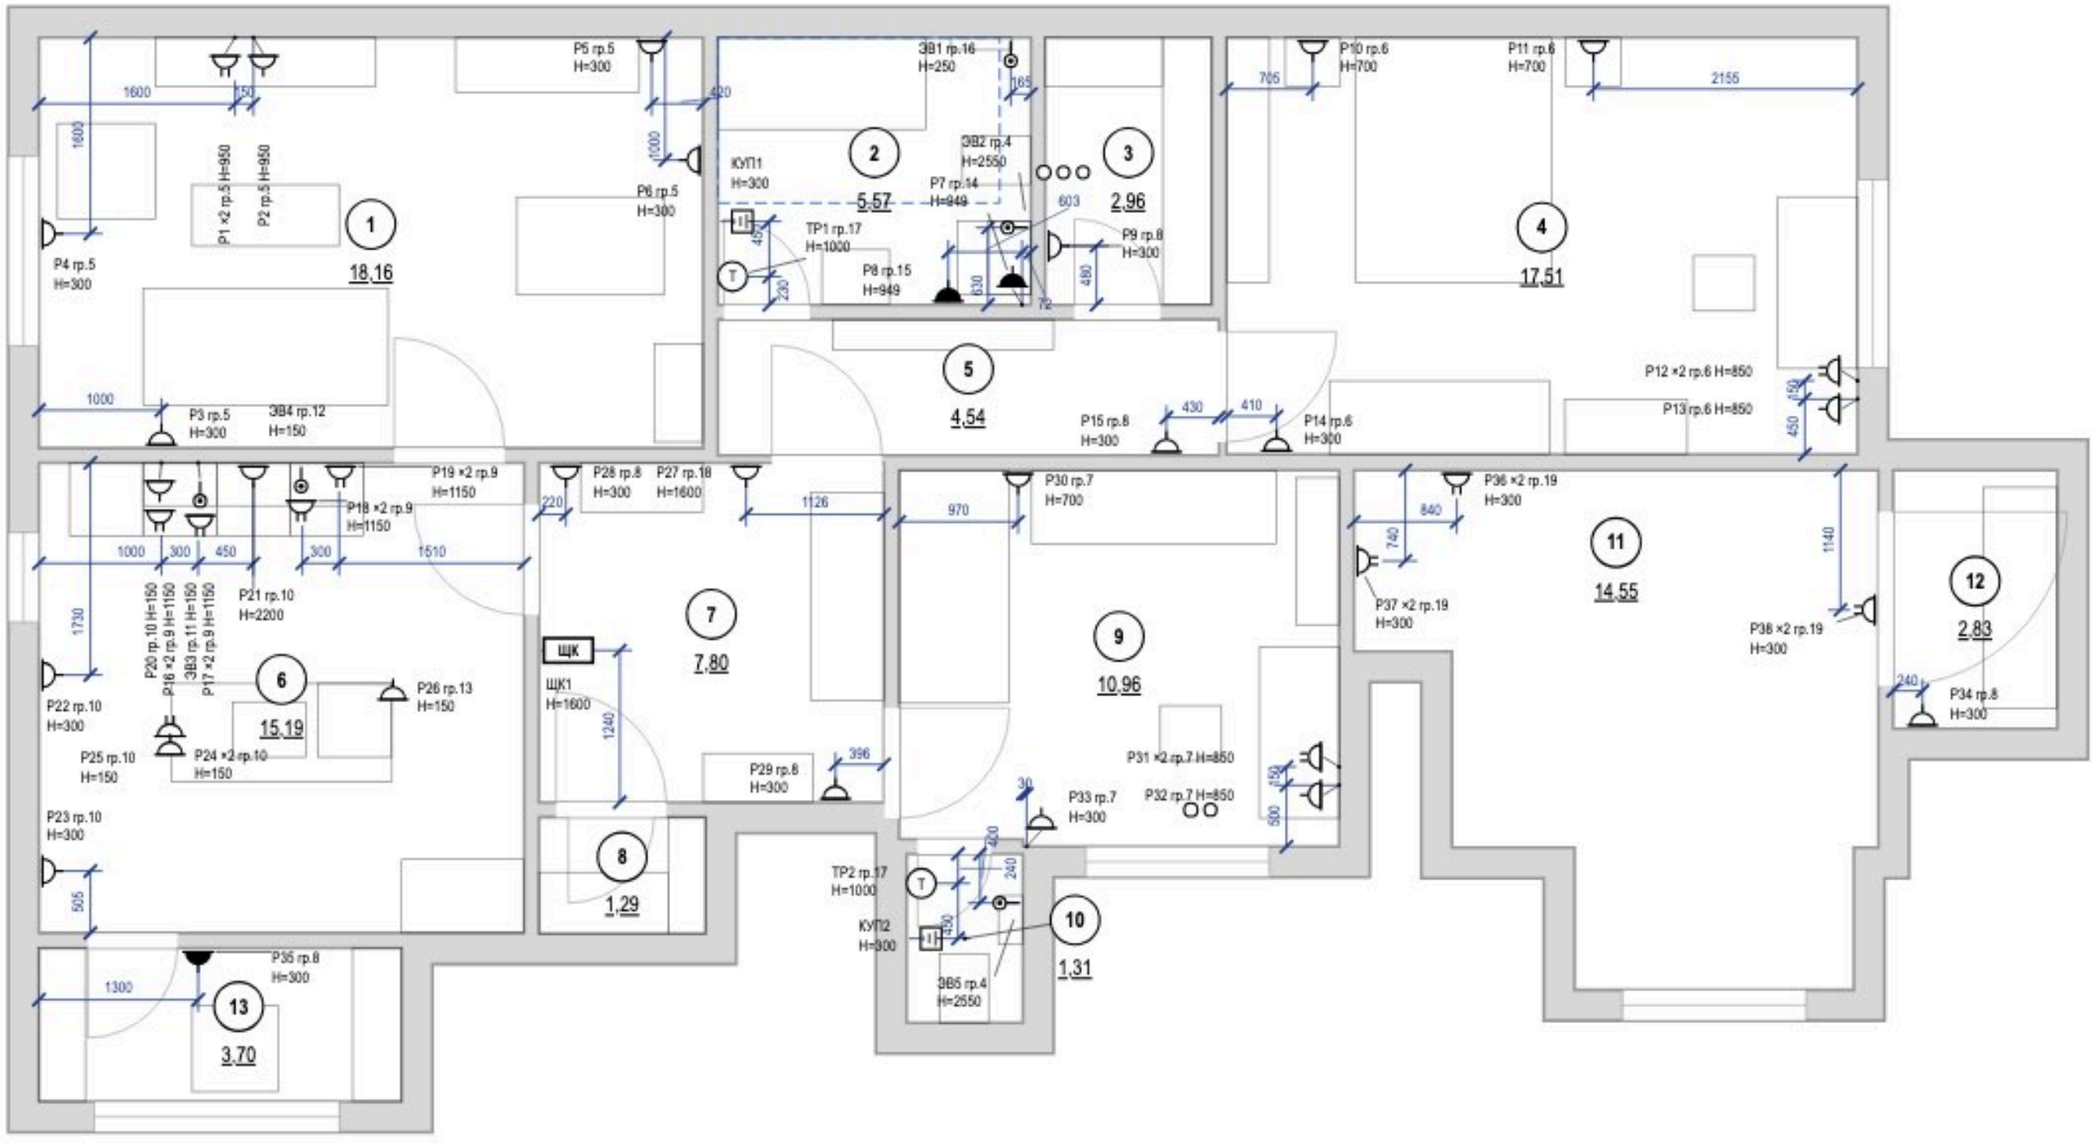


Примечания

1. За отметку 0,000 принят уровень чистого пола. Высоты H — от чистого пола до оси изделия; привязки — от чистовой грани стены до оси механизма (у рамки на нескольких постов — до оси рамки).
2. Высота установки, не указанная на плане: розетки — 300 мм от чистого пола; выводы кабеля — по паспорту прибора.
3. Розетки в санузле — только вне зон 0–2 (ПУЭ 7.1.48, ГОСТ Р 50571.7.701-2024), IP44, через УЗО 30 мА.
4. Розеточные и мокрые линии — через УЗО или дифавтомат с током утечки не более 30 мА (ПУЭ 7.1.79); в санузле выполнить ДСУП (ПУЭ 7.1.87–7.1.88).
5. Кабель — медный, исполнение нг(A)-LS (ГОСТ 31565-2012); скрытая прокладка только горизонтально и вертикально, фактические трассы зафиксировать исполнительной схемой до закрытия отделкой.
6. Расчёт нагрузок, токов КЗ, селективности и сечений — по проекту ЭОМ организации с допуском СРО; лист задаёт состав, расположение и группы.
7. Ведомости электроточек, изделий, светильников и расшифровка клавиш — лист «Ведомость электроточек и изделий».

					Проект: Четырёхкомнатная квартира
	Лист	№ док.	Подпись	Дата	
Дизайнер	Кырпан А.С.			05.10.26	План розеток и электровыводов
					Стадия: П; Лист: 26; Листов: 111

выпуск 05.10.2026 № d0efc1af8a · стр. 26 из 111

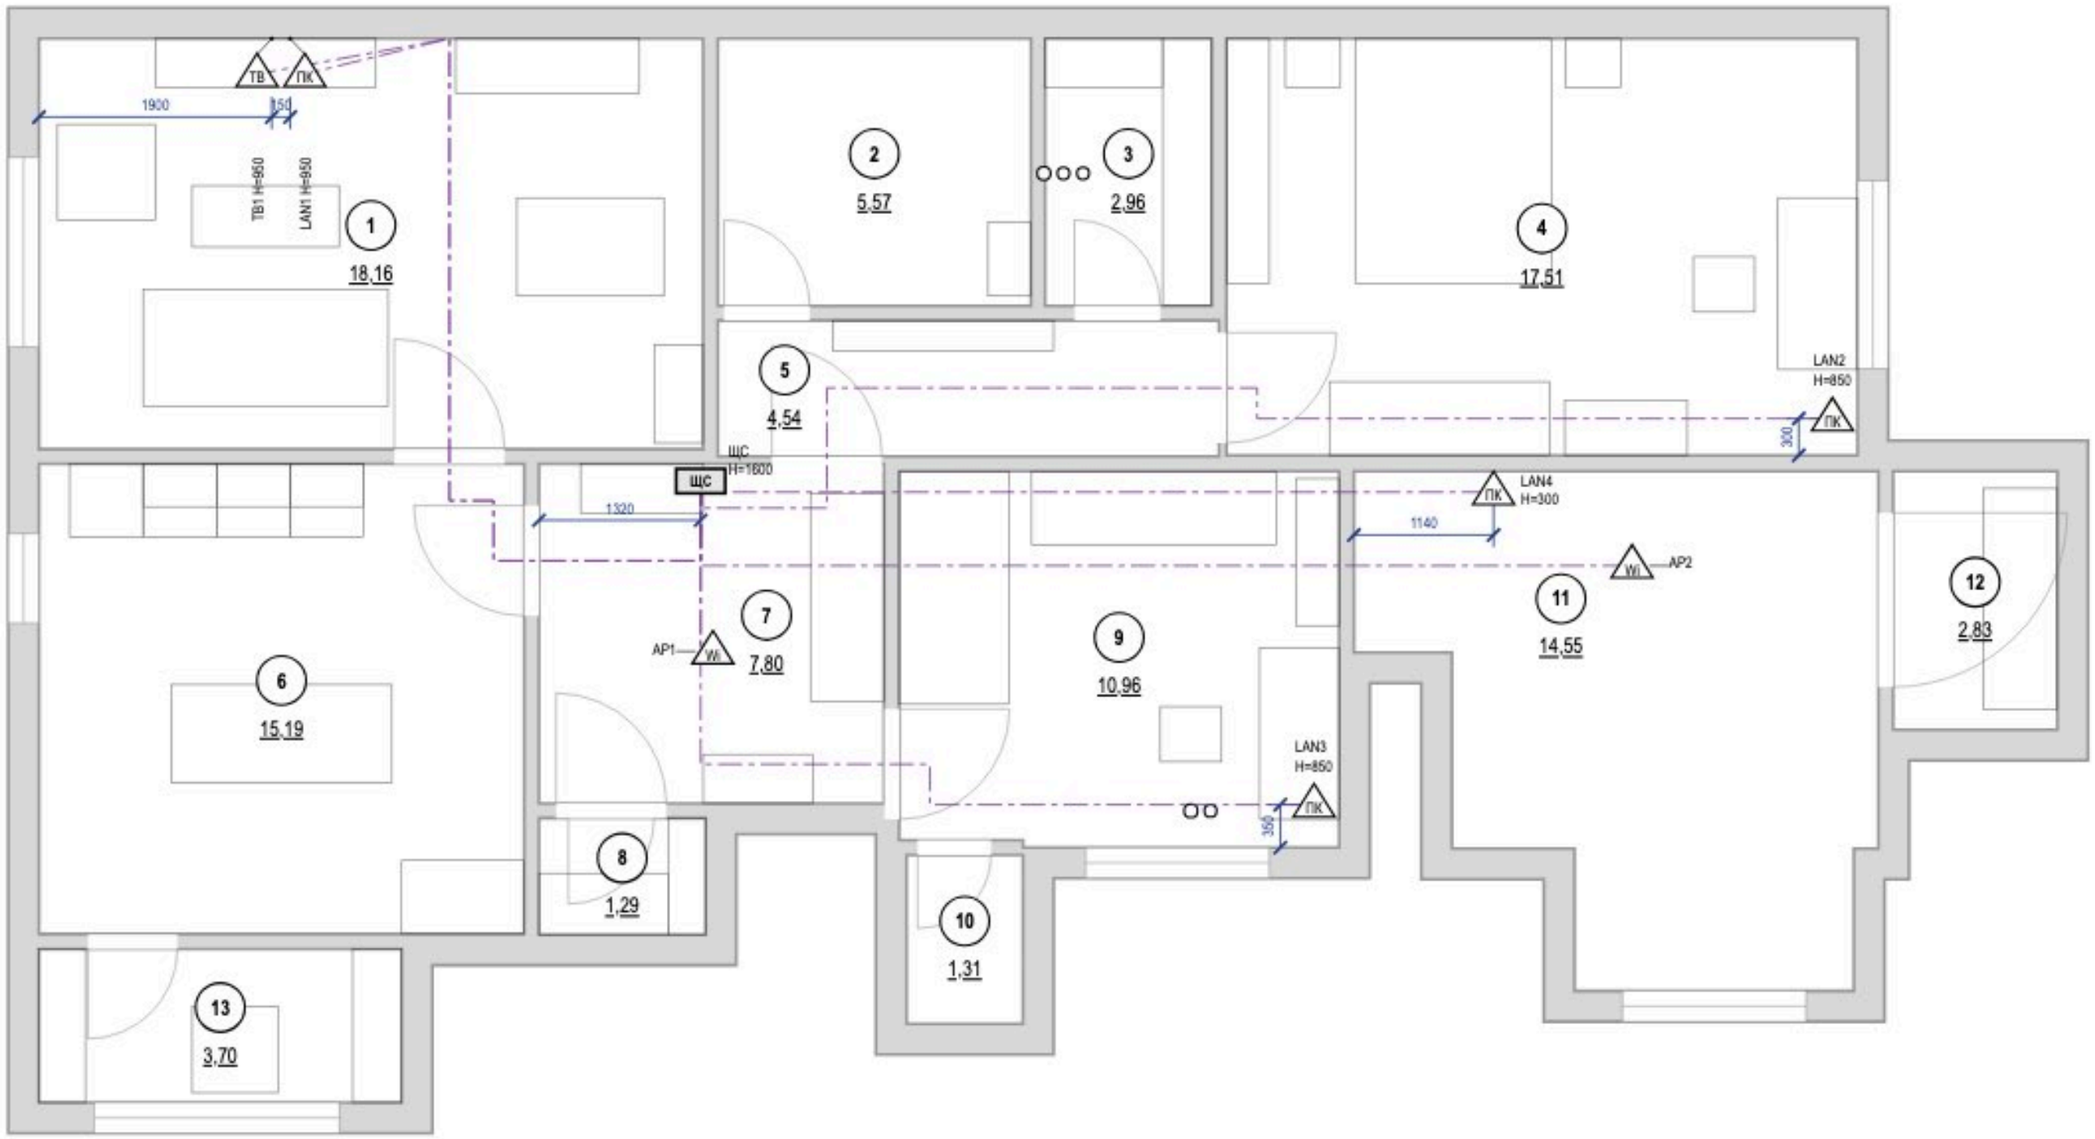


Примечания

1. За отметку 0,000 принят уровень чистого пола. Высоты H — от чистого пола до оси изделия; привязки — от чистовой грани стены до оси механизма (у рамки на нескольких постов — до оси рамки).
2. Высота установки, не указанная на плане: розетки LAN и ТВ — 300 мм от чистого пола.
3. Слаботочные кабели — отдельно от силовых: в своей трубе или лотке, при параллельной прокладке не ближе 100 мм к силовым, пересечения под прямым углом; каждую точку — отдельным кабелем от ЩС без скруток.
4. Трассы на листе — принципиальные; фактические зафиксировать исполнительной схемой до закрытия отделки. Силовые линии, УЗО 30 мА, ДСУП, кабель нг(A)-LS — по листам розеток и щита.
5. Проект силовой части и расчёт токов КЗ — по проекту ЭОМ; слаботочная часть согласуется с провайдером и управляющей компанией (домофон, коллективное ТВ).

					Проект: Четырёхкомнатная квартира
	Лист	№ док.	Подпись	Дата	
Дизайнер	Кырпан А.С.			05.10.26	План слаботочных сетей
					Стадия: П; Лист: 27; Листов: 111

выпуск 05.10.2026 · d0efc1af8a · стр. 27 из 111

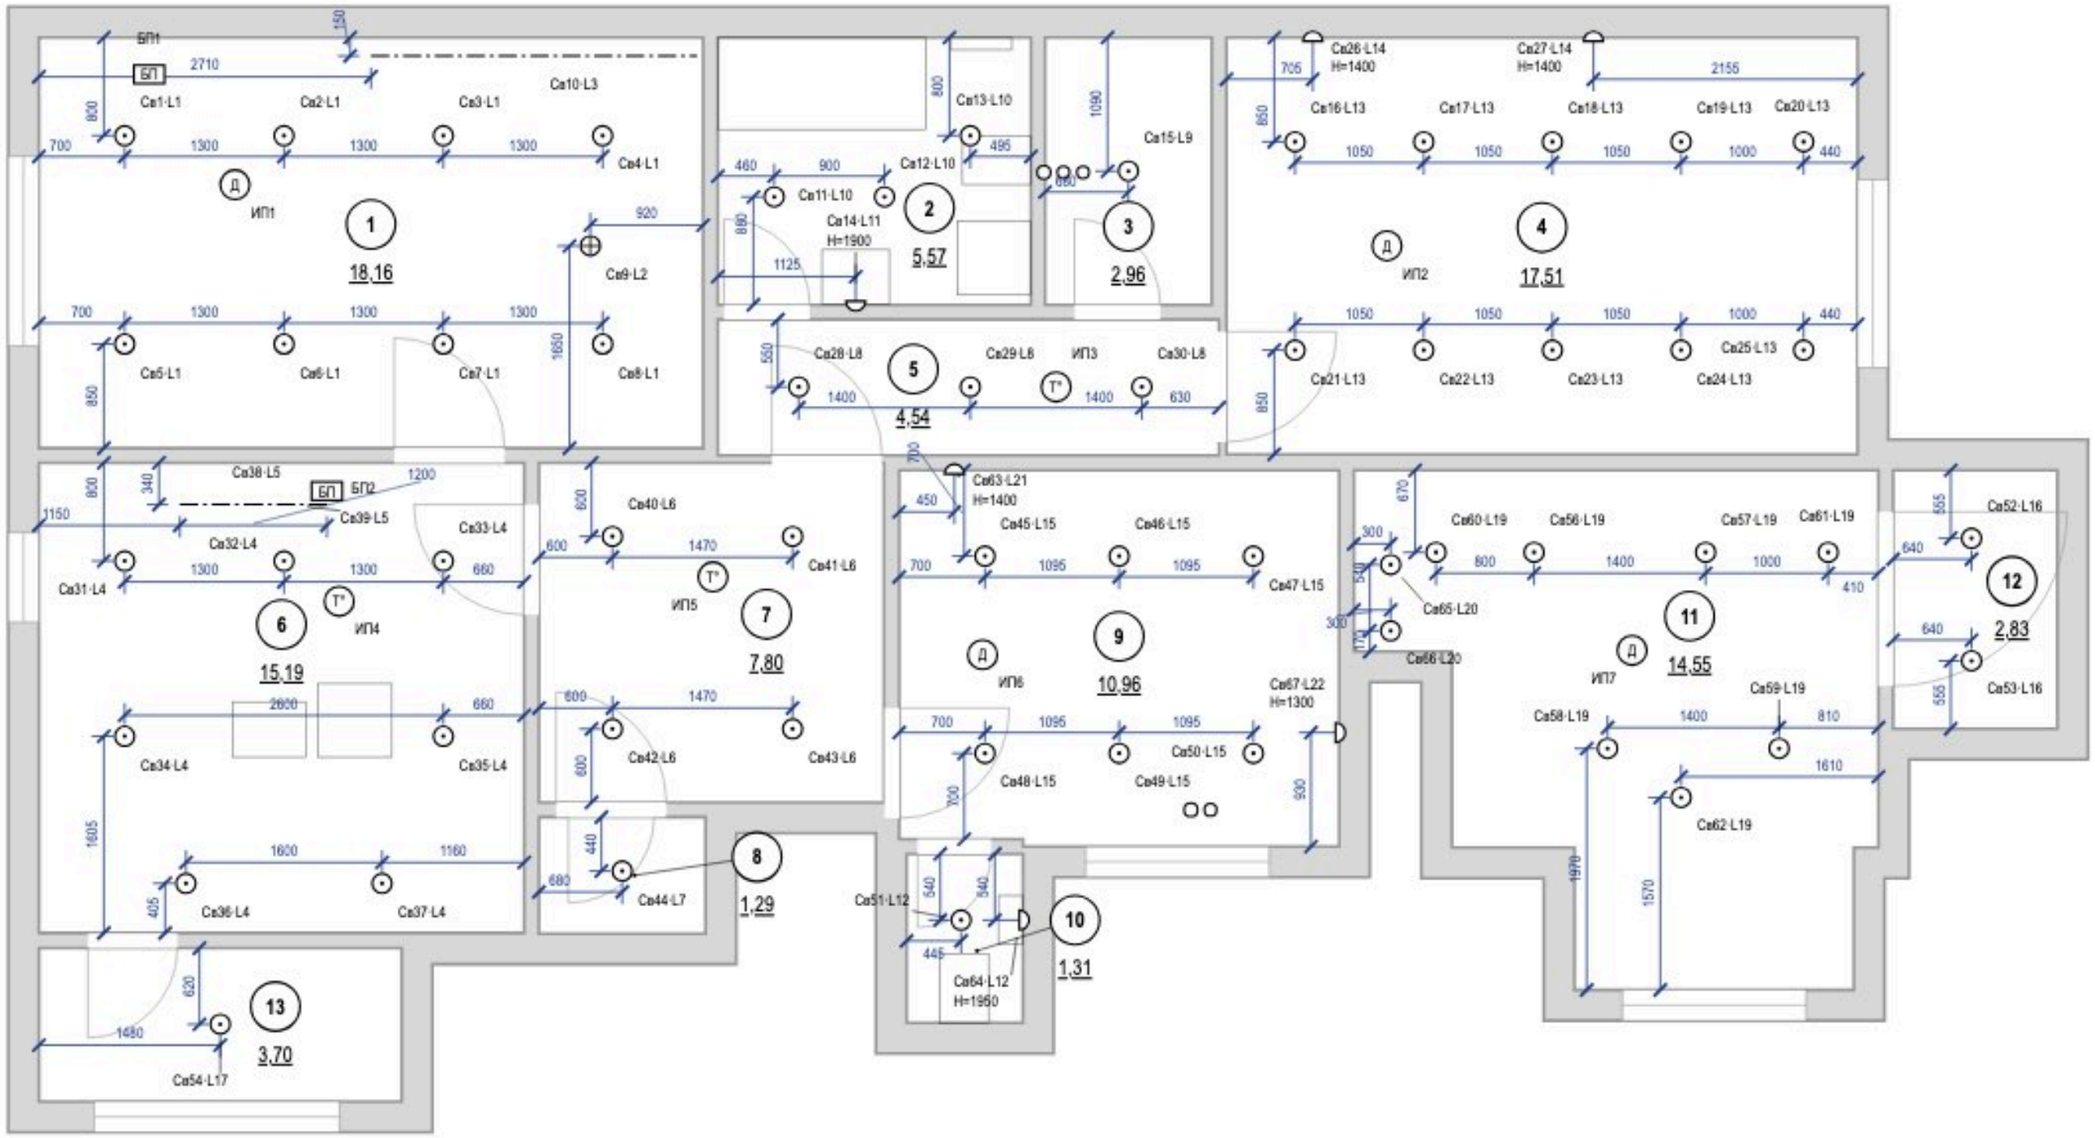

Примечания

1. За отметку 0,000 принят уровень чистого пола. Высоты H — от чистого пола до оси изделия; привязки — от чистовой грани стены до оси механизма (у рамки на несколько постов — до оси рамки).
2. Высота установки, не указанная на плане: светильники — на потолке; настенные — по отметке H у знака. Привязки — до оси светильника от чистовой грани стены, по рядам.
3. Освещённость: Eн — СанПиН 1.2.3685-21, табл. 5.52 (на полу); Φ треб. = Eн·S/(U·MF) при U = 0,5 и MF = 0,71 (СП 52.13330.2016, табл. 4.3) — оценка, не светотехнический расчёт. Декоративная подсветка в Φ не входит.
4. Во влажных помещениях — светильники не ниже IP44; в зонах 0–2 ванной — по ГОСТ Р 50571.7.701-2024 (зона 1 — IPX5).
5. Розеточные и мокрые линии — через УЗО или дифавтомат с током утечки не более 30 мА (ПУЭ 7.1.79); в санузле выполнить ДСУП (ПУЭ 7.1.87–7.1.88).
6. Кабель — медный, исполнение нг(A)-LS (ГОСТ 31565-2012); скрытая прокладка только горизонтально и вертикально, фактические трассы зафиксировать исполнительной схемой до закрытия отделкой.
7. Расчёт нагрузок, токов КЗ, селективности и сечений — по проекту ЭОМ организации с допуском СРО; лист задаёт состав, расположение и группы.
8. Ведомость светильников — лист «Ведомость электроточек и изделий».

					Проект: Четырёхкомнатная квартира			
	Лист	№ док.	Подпись	Дата	План освещения	Стадия	Лист	Листов
Дизайнер	Кырпан А.С.			05.10.26		П	28	111

выпуск 05.10.2026 · d0efc1af8a · стр. 28 из 111

Спецификация светильников

Поз.	Марки	Наименование	Установка	Кол.	P, Вт	Σ P, Вт	Ф, лм	Тц, K	Ra	Угол, °	IP	Дим.	Группа	Пом.
1	Св1–Св8, Св16–Св19, Св20, Св21–Св24, Св25, Св31–Св37, Св56–Св62	Встраиваемый точечный	в ГКЛ, корпус ≤ 70 мм	32	12	384	1000	3000	90	—	20	—	L1, L4, L13, L19	1, 4, 6, 11
2	Св9	Подвесной	подвес, низ H=1600	1	15	15	1200	2700	90	—	20	—	L2	1
3	Св10	Лента светодиодная 24 В	в коробе, профиль с рассеивателем	5 м	9,6/м	48	900/м	2700	90	—	20	да	L3	1
4	Св11, Св12, Св13, Св51	Встраиваемый точечный	в ГКЛ, корпус ≤ 70 мм	4	6	24	500	3000	90	—	44	—	L10, L12	2, 10
5	Св14, Св64	Светильник над зеркалом, драйвер встроен	над зеркалом, H=1900, 1950	2	8	16	600	3000	90	—	44	—	L11, L12	2, 10
6	Св15, Св40–Св44, Св52, Св53, Св65, Св66	Встраиваемый точечный	в ГКЛ, корпус ≤ 70 мм	10	6	60	500	3000	90	—	20	—	L6, L7, L9, L16, L20	3, 7, 8, 11, 12
7	Св26, Св27, Св63	Настенный (бра)	на стене, H=1400	3	6	18	400	2700	90	60	20	—	L14, L21	4, 9
8	Св28–Св30	Встраиваемый точечный	в ГКЛ, корпус ≤ 70 мм	3	5	15	400	3000	90	—	20	—	L8	5
9	Св38, Св39	Линейный светильник	на поверхности	1,2 м	8	16	700	3000	90	—	20	—	L5	6
10	Св45–Св50	Встраиваемый точечный	в ГКЛ, корпус ≤ 70 мм	6	13	78	1100	3000	90	—	20	—	L15	9
11	Св67	Бра подсветки рабочего места, стол M_35	на стене, H=1300	1	7	7	450	3000	90	60	20	—	L22	9
12	Св54	Встраиваемый точечный	в ГКЛ, корпус ≤ 70 мм	1	9	9	800	3000	90	—	44	—	L17	13
		Итого		**63 шт + 6,2 м**		**690**								

LED-ленты, линейные светильники и блоки питания

Марка	Пом.	L, м	U, В	Вт/м	Σ P, Вт	БП	P БП, Вт	Загр., %	Питание	Доступ к БП
Св10	1	5	24	9,6	48	БП1	100	48	с одного конца	люк 300×300 в коробе потолка у стены A
Св38	6	0,6	24	—	8	БП2	30	53	встроенный ввод	в навесном модуле M_25, съёмная панель
Св39	6	0,6	24	—	8	БП2	30	53	встроенный ввод	в навесном модуле M_25, съёмная панель

Сценарии освещения

Пом.	Сценарий	Группы и уровни, %	Чем включается
1	Вечер	L1 общий свет (споты) — 0; L2 подвес над обеденным столом — 100; L3 лента в карнизе (диммер) — 50	S1, S2 светорегулятор
1	Гости	L1 общий свет (споты) — 100; L2 подвес над обеденным столом — 100; L3 лента в карнизе (диммер) — 100	S1, S2 светорегулятор
1	Кино	L1 общий свет (споты) — 0; L2 подвес над обеденным столом — 0; L3 лента в карнизе (диммер) — 20	S2 светорегулятор
1	Уборка	L1 общий свет (споты) — 100; L2 подвес над обеденным столом — 100; L3 лента в карнизе (диммер) — 0	S1

Слои света

общий — равномерный свет помещения, по норме освещённости

рабочий — местный свет задачи: столешница, зеркало, чтение у кровати

акцентный — подсветка потолка, стен и ниш; не входит в поток общего света

Слои света по помещениям


Пом.	Помещение	Слои света и группы включения (марки светильников)	Тц, K	Ra	Σ P, Вт	Сцен.
1	Зал	общий — L1 (Св1–Св8); рабочий — L2 (Св9); акцентный — L3 (Св10)	2700 / 3000	90	159	4
2	Ванная комната	общий — L10 (Св11, Св12, Св13); рабочий — L11 (Св14)	3000	90	26	—
3	Тёмная комната	общий — L9 (Св15)	3000	90	6	—
4	Детская 1	общий — L13 (Св16–Св19, Св20, Св21–Св24, Св25); рабочий — L14 (Св26, Св27)	2700 / 3000	90	132	—
5	Коридор	общий — L8 (Св28–Св30)	3000	90	15	—
6	Кухня	общий — L4 (Св31–Св37); рабочий — L5 (Св38, Св39)	3000	90	100	—
7	Прихожая-коридор	общий — L6 (Св40–Св43)	3000	90	24	—
8	Гардеробная 2	общий — L7 (Св44)	3000	90	6	—
9	Детская 2	общий — L15 (Св45–Св50); рабочий — L21 (Св63), L22 (Св67)	2700 / 3000	90	91	—
10	Санузел	общий — L12 (Св51); рабочий — L12 (Св64)	3000	90	14	—
11	Гостиная	общий — L19 (Св56–Св62); акцентный — L20 (Св65, Св66)	3000	90	96	—
12	Гардеробная 1	общий — L16 (Св52, Св53)	3000	90	12	—
13	Балкон 1	общий — L17 (Св54)	3000	90	9	—

Примечания

1. Позиции и марки Св — те же, что на плане освещения (лист 28) и в ведомости светильников (лист «Ведомость электроточек и изделий»); группы L — по плану выключателей (лист 30).
2. Модели светильников не назначены: подбор по графам спецификации — поток, Тц, Ra, угол, IP и диммирование не хуже указанных, мощность не больше; встраиваемые — под глубину короба (графа «Установка»). IP 20 — сухие помещения.
3. Длина LED-ленты в карнизе — по линии карниза плана потолков (лист 24); Σ P = Вт/м × длина. Блок питания загружен не больше чем на 80 %; лента 24 В длиннее 10 м питается с двух концов; доступ к блоку питания — люк ревизии 300×300 мм или место, указанное в таблице.
4. Сценарии: уровень — доля максимальной яркости группы, %; 0 — группа выключена. Уровень ниже 100 % — только у групп на светорегуляторе (задний фронт, ТЕ) с диммируемыми драйверами и блоками питания.
5. Мощность и поток — по паспортам принятых изделий, Σ P — установленная мощность освещения. Оценка освещённости — на плане освещения; это не светотехнический расчёт.

					Проект: Четырёхкомнатная квартира			
	Лист	№ док.	Подпись	Дата				
Дизайнер	Кырпан А.С.			05.10.26	Спецификация светильников и сценарии освещения	Стадия	Лист	Листов
						П	29	111

выпуск 05.10.2026 № d0efc1af8a · стр. 29 из 111

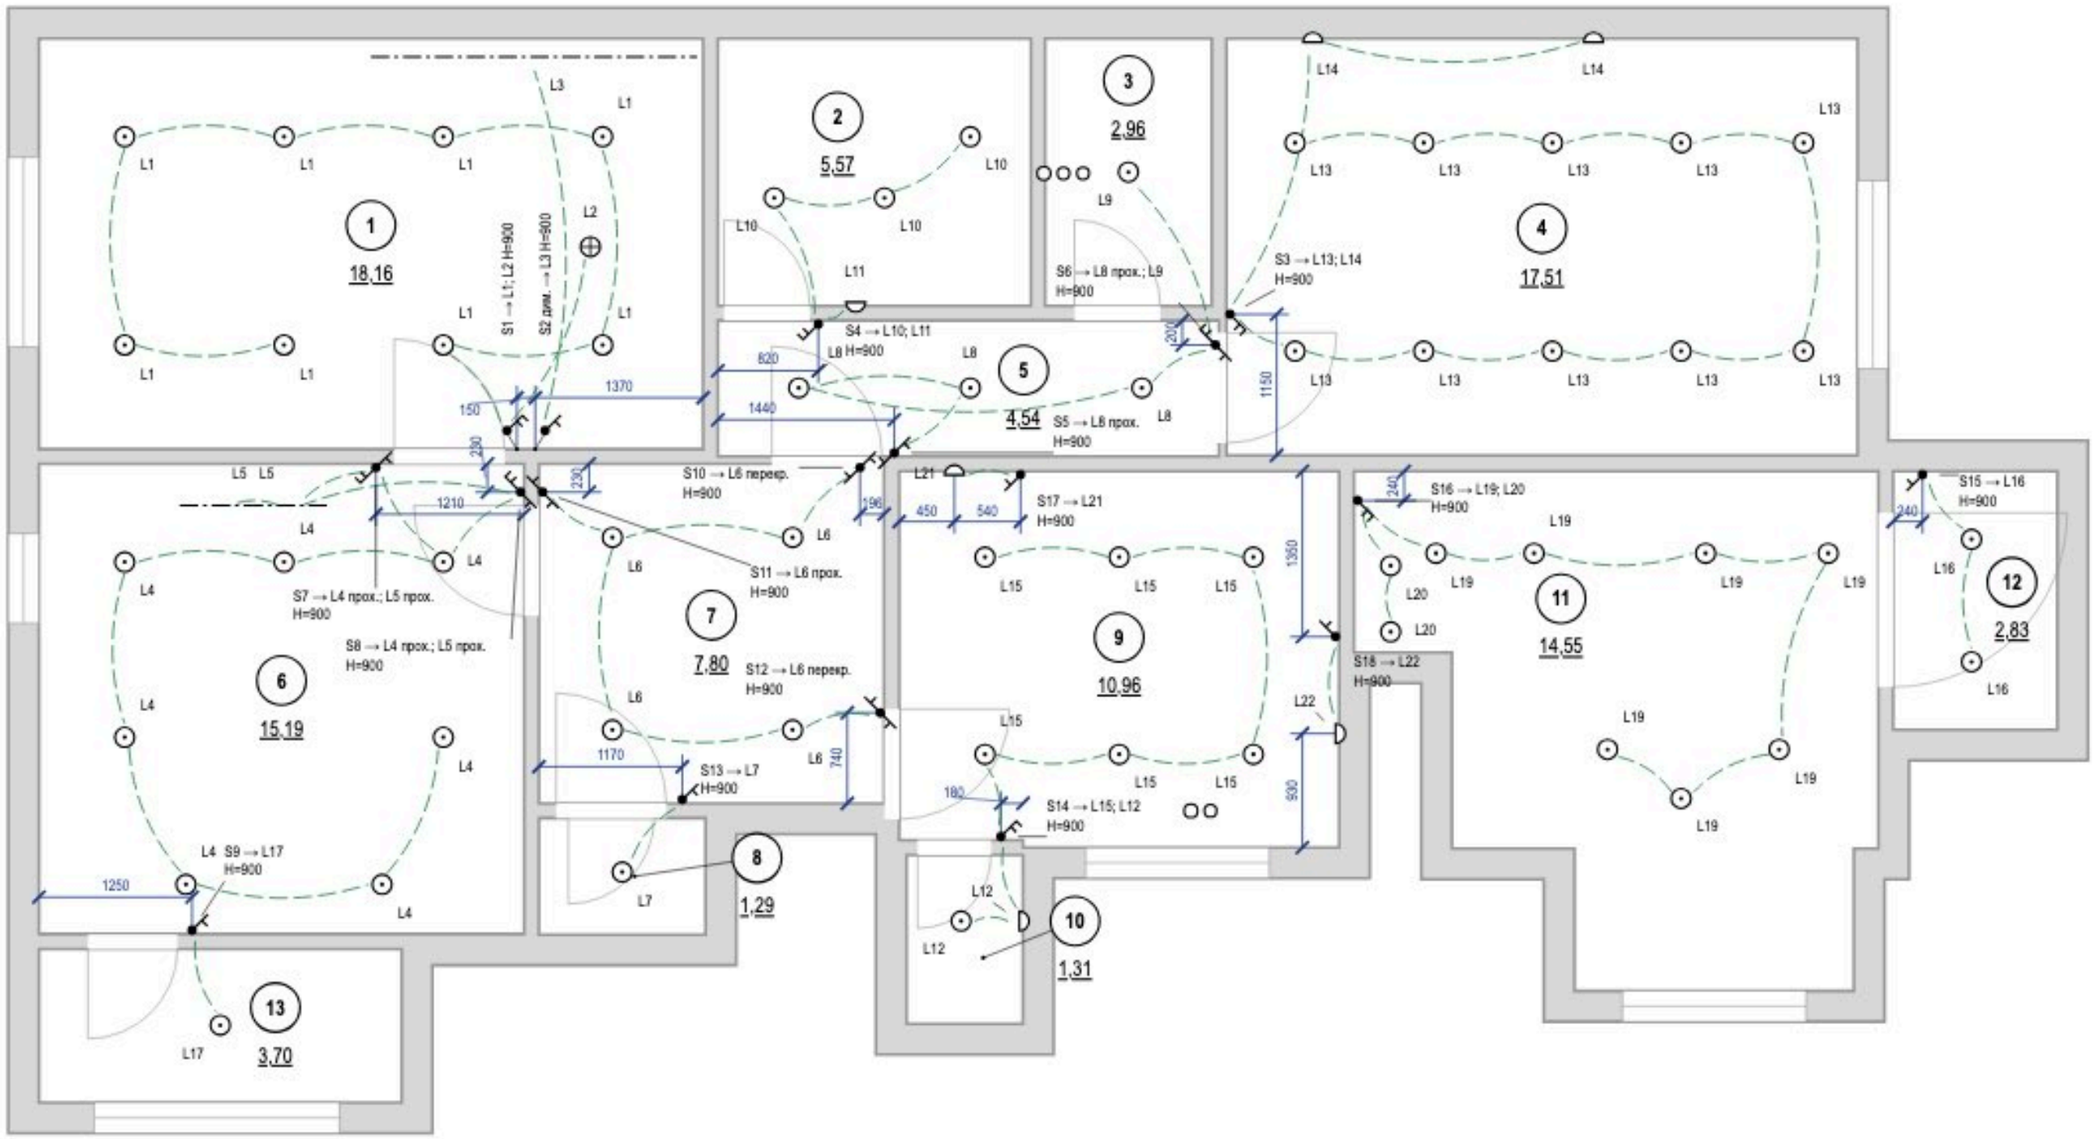

Примечания

1. За отметку 0,000 принят уровень чистого пола. Высоты H — от чистого пола до оси изделия; привязки — от чистовой грани стены до оси механизма (у рамки на несколько постов — до оси рамки).
2. Высота установки, не указанная на плане: выключатели — 900 мм от чистого пола, со стороны дверной ручки (ПУЭ 7.1.51).
3. Линии связи показывают, какой выключатель какую группу L включает; это не трасса кабеля. Трасса — принципиальная, фактическую зафиксировать исполнительной схемой.
4. Группы из нескольких мест (L8 — S5, S6; L4 — S7, S8; L5 — S7, S8; L6 — S10, S11, S12): на крайних местах — проходные клавиши, на промежуточных перекрёстные; механизмы — в ведомости изделий.
5. Светорегулятор — по заднему фронту (для LED-драйверов), совместимость с драйверами проверить до закупки.
6. Розеточные и мокрые линии — через УЗО или дифавтомат с током утечки не более 30 мА (ПУЭ 7.1.79); в санузле выполнить ДСУП (ПУЭ 7.1.87–7.1.88).
7. Кабель — медный, исполнение нг(A)-LS (ГОСТ 31565-2012); скрытая прокладка только горизонтально и вертикально, фактические трассы зафиксировать исполнительной схемой до закрытия отделкой.
8. Расчёт нагрузок, токов КЗ, селективности и сечений — по проекту ЭОМ организации с допуском СРО; лист задаёт состав, расположение и группы.
9. Расшифровка клавиш и ведомость изделий — лист «Ведомость электроточек и изделий».

					Проект: Четырёхкомнатная квартира
	Лист	№ док.	Подпись	Дата	Управление светильниками
Дизайнер	Кырпан А.С.			05.10.26	

Стадия	Лист	Листов
П	30	111

выпуск 05.10.2026 · d0efc1af8a · стр. 30 из 111



Примечания

1. Расчёт систем ОВ и подбор оборудования — проектная организация с допуском СРО; лист даёт места, трассы и привязки.
2. Нормы вытяжки — СП 54.13330.2022 (Изм. 1, 2), табл. 7.1: кухня с электроплитой 60 м³/ч, с газовой 100; ванная и совмещённый санузел 50; уборная 25; гардеробная 0,2 ч⁻¹. Приток в жилые — 3 м³/ч на 1 м² (менее 20 м² общей площади на человека), иначе 30 м³/ч на человека.
3. Вентканалы и шахты не сужать, не переносить и не закрывать; вентилятор и кухонная вытяжка — через обратный клапан, без перекрытия естественной тяги.
4. Проектные расходы — не ниже нормы, вытяжка сведена с притоком вентиляторами мокрых помещений. Клапаны — в простенке у окна, центр 2000 мм, не над кроватью, не ближе 300 мм к стоякам отопления; типоразмер — на расход.
5. Под подшивным потолком вытяжка — в потолке, воздуховодом за потолком до канала. Кухонная вытяжка в воздухообмен не включена: воздуховод не менее Ø125 в коробе, вход в канал отдельный.
6. Переток — зазор под полотнами межкомнатных дверей или переточная решётка.
7. Кондиционирование заданием не предусмотрено; при установке трассы фреона и дренажа (не менее 40 мм/м, в К1 через сифон) и питание заложить до черновых работ.
8. Привязки оборудования — по паспортам приобретённых моделей, до черновых работ.

					Проект: Четырёхкомнатная квартира
	Лист	№ док.	Подпись	Дата	
Дизайнер	Кырпан А.С.			05.10.26	План вентиляции

Стадия	Лист	Листов
П	31	111

выпуск 05.10.2026 · d0efc1af8a · стр. 31 из 111



Примечания

1. Расчёт системы отопления, теплопотерь и подбор приборов — проектная организация с допуском СРО; лист даёт места и привязки.
2. Тип, длина и мощность радиаторов — по теплотехническому расчёту; лист задаёт места, зазоры и подключение.
3. Радиаторы — под каждым окном жилых комнат и кухни, центр по оси проёма, длина 0,7 ширины окна (кратно 100); окончательно — по расчёту.
4. Зазоры радиатора: низ не менее 100 мм от чистого пола, верх не менее 100 мм до подоконника, 30–50 мм от стены до задней панели; центр по оси окна с допуском ±20 мм.
5. Радиаторы не закрывать глухими коробами и мебелью; перенос и замена приборов в многоквартирном доме — переустройство, согласование с управляющей организацией (ЖК РФ ст. 25–26); вынос на лоджию запрещён.
6. Трубы отопления через межквартирные стены не прокладывать (СП 51.13330.2011, п. 9.19); через перекрытия и перегородки — в гильзах.
7. Привязки приборов и подводок — по паспортам приобретённых радиаторов и клапанов, до черновых работ.
8. До закрытия отделкой трубопроводы отопления испытать гидростатическим давлением с оформлением акта (СП 73.13330.2016, 7.2–7.3).

					Проект: Четырёхкомнатная квартира
	Лист	№ док.	Подпись	Дата	План отопления
Дизайнер	Кырпан А.С.			05.10.26	

Стадия	Лист	Листов
П	32	111


выпуск 05.10.2026 · d0efc1af8a · стр. 32 из 111

Спецификация плинтусов

Наименование	Помещения	Длина, м (с запасом)
Плинтус МДФ под окраску 80×16 мм, крепление к стене, окраска в цвет Tikkurila F497	1, 3, 4, 5, 6, 7, 8, 9, 11, 12	117
Плинтус из керамогранита пола, подрезка 80 мм, верхняя кромка с запилом 45°, h = 80 мм, крепление к стене	13	9

Отметки по высоте

±0,000	чистый пол пом. 1, 3–9, 11, 12; отсчёт высот
−0,015	чистый пол пом. 2, 10, ниже на 15 мм
−0,030	чистый пол пом. 13, ниже на 30 мм
−0,170	верх плиты — расчёт, не замер (задание на обмер)
сущ. пол	снимается до плиты; не замерен (задание на обмер)

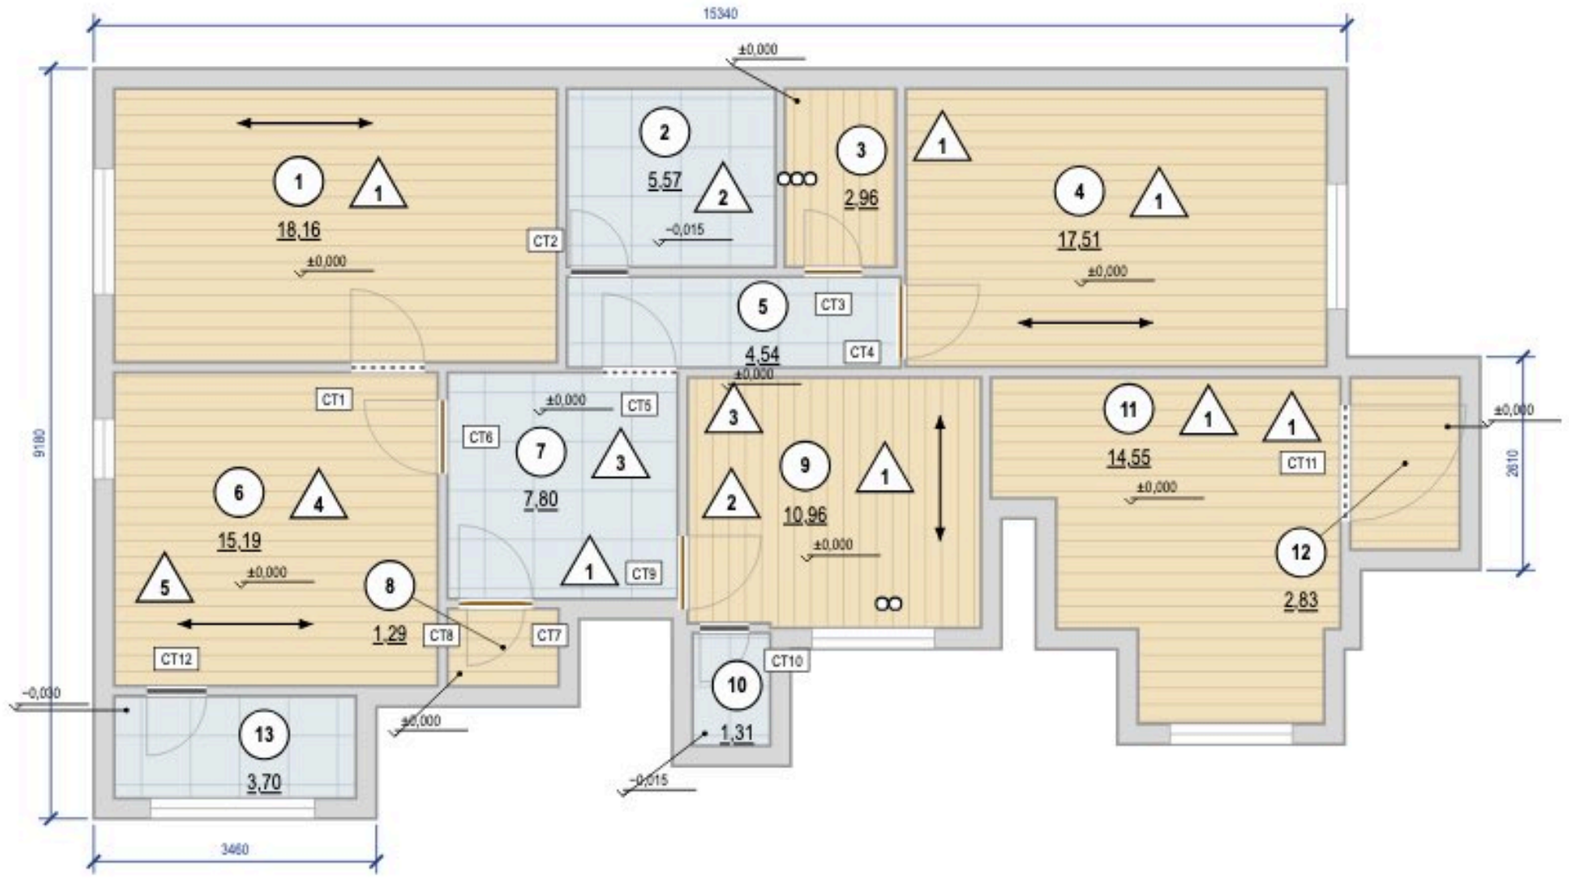

Экспликация полов

Номер помещения	Тип пола	Схема пола	Данные элементов пола (наименование, толщина, основание), мм	Площадь, м²
1, 3, 4, 8, 9, 11, 12	1		Инженерная доска дуб на клею — 14 Клей паркетный МС-полимерный — 1 Стяжка ЦПС М300 (В22,5), фибра, по звукоизоляции — 55 Звукоизоляция — минплита 110 кг/м³ 20 Засыпка керамзитовая фр. 0–5, уплотнённая — 80 Плита перекрытия монолитная Всего 170 мм; ЧП ±0,000, верх плиты −0,170	68,26
2, 10	2		Керамогранит 600×600×10 — 10 Нагревательный мат в слое клея C2 TE S1 — 8 Гидроизоляция обмазочная, 2 слоя (заход на стены — по ведомости отделки) — 2 Сборное основание ГВЛВ 2×12,5 — 25 Засыпка керамзитовая сухая фр. 0–5 (в слое — выпуски К1) — 110 Плита перекрытия монолитная Всего 155 мм; ЧП −0,015, верх плиты −0,170	6,88
5, 7	3		Керамогранит 600×600×10 — 10 Клей плиточный C2 TE S1 — 5 Стяжка ЦПС М300 (В22,5), фибра, по звукоизоляции — 55 Звукоизоляция — минплита 110 кг/м³ 20 Засыпка керамзитовая фр. 0–5, уплотнённая — 80 Плита перекрытия монолитная Всего 170 мм; ЧП ±0,000, верх плиты −0,170	12,34
6	4		Инженерная доска дуб на клею — 14 Клей паркетный МС-полимерный — 1 Гидроизоляция полиуретановая, 2 слоя (зона мойки и острова) — 2 Стяжка ЦПС М300 (В22,5), фибра, по звукоизоляции — 53 Звукоизоляция — минплита 110 кг/м³ 20 Засыпка керамзитовая фр. 0–5, уплотнённая — 80 Плита перекрытия монолитная Всего 170 мм; ЧП ±0,000, верх плиты −0,170	15,19
13	5		Керамогранит 600×600×10 — 10 Клей плиточный C2 TE S1 (деформируемый) — 5 Сборное основание ГВЛВ 2×12,5 — 25 Пенополистирол экструзионный 2×50 100 Плита перекрытия монолитная Всего 140 мм; ЧП −0,030, верх плиты −0,170	3,70
			Итого	**106,37**


Примечания

1. За отметку ±0,000 принят чистый пол, не существующий (блок отметок). Площади — по чистым размерам помещений, м²; размеры — в мм.
2. Стык разнотипных покрытий — по оси дверного полотна (под полотном в закрытом положении); решение стыка — по ведомости стыков.
3. Пол санузлов ниже смежных помещений на 15 мм за счёт меньшей толщины стяжки (верх плиты общий — по экспликации полов); гидроизоляция по стяжке с заведением на стены не менее 200 мм (СП 29.13330.2011, п. 7.2), до облицовки — тест проливом и акт скрытых работ.
4. Выпуски канализации с уклоном и трассы водоснабжения — в слое засыпки под стяжкой (по экспликации полов); отметки, уклоны и прочистки — по листу разводки ВК 19.
5. Штучные покрытия (инженерная доска): направление — по стрелке; влажность основания по СМ не более 2,0 % (по ТУ изготовителя).
6. Ровность основания — просвет под 2-метровой рейкой не более 2 мм: пом. 1, 3, 4, 6, 8, 9, 11, 12 (инженерная доска), пом. 2, 5, 7, 10 (керамогранит); 3 мм: пом. 13 (керамогранит); проверить до укладки покрытия (СП 71.13330.2017, табл. 8.5).
7. Плавающая стяжка по звукоизоляции: демпферная (кромочная) лента по контуру помещения, у стояков и колонн — до верха чистого пола (СП 51.13330.2011, п. 9.11); плинтус крепится только к стене.
8. Сетка на плитке — условная, в размер формата; точка старта и раскладка — по листу раскладки плитки.
9. Пироги полов — по экспликации полов: слои сверху вниз, толщины в мм; гидроизоляция мокрых зон — в пироге и в ведомости отделки; схема пола — без масштаба.


					Проект: Четырёхкомнатная квартира
	Лист	№ док.	Подпись	Дата	План покрытий пола
Дизайнер	Кырпан А.С.			05.10.26	Стадия: П; Лист: 33; Листов: 111

выпуск 05.10.2026 № d0efc1af8a · стр. 33 из 111


Фрагмент 1. Ванная комната (пом. 2). Пол 600×600, шов 2 мм, М 1:40

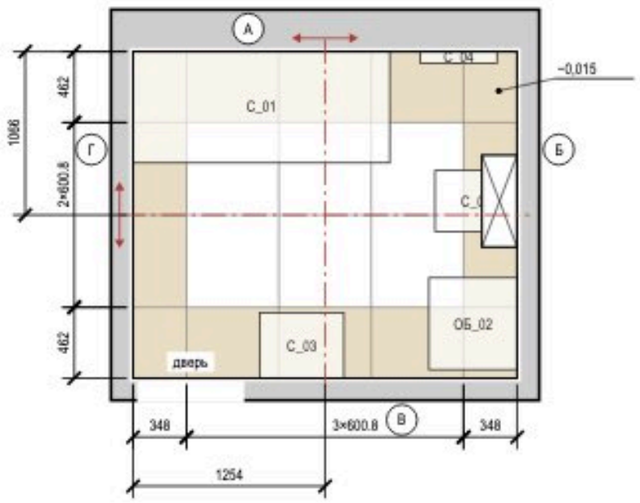


Фрагмент 2. Коридор (пом. 5). Пол 600×600, шов 2 мм, М 1:40

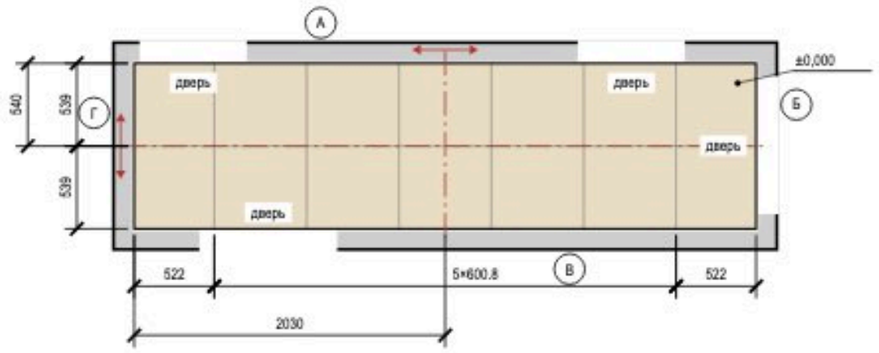

Фрагмент 3. Прихожая-коридор (пом. 7). Пол 600×600, шов 2 мм, М 1:40

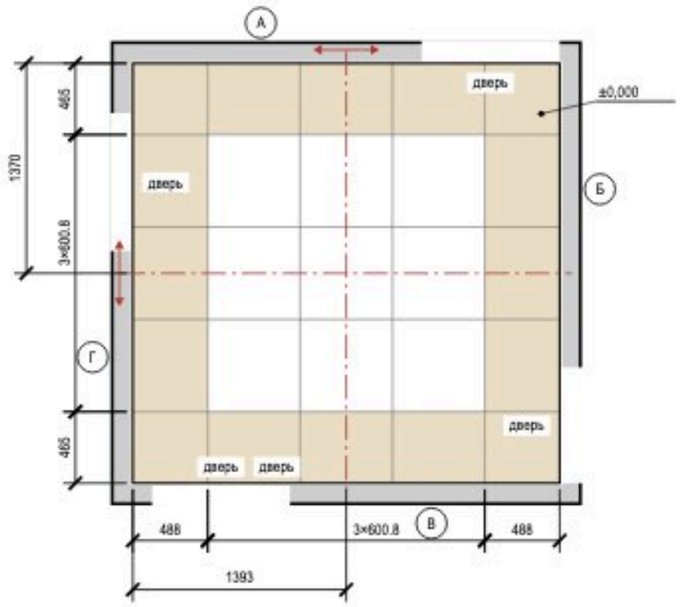

Фрагмент 4. Санузел (пом. 10). Пол 600×600, шов 2 мм, М 1:40

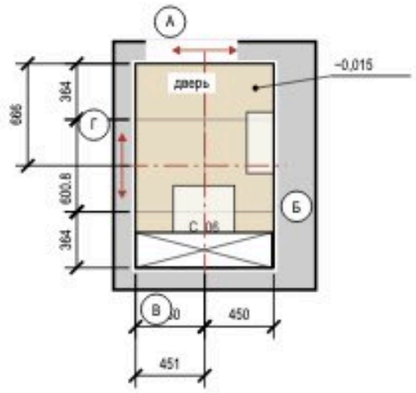

Условные обозначения

- плитка целая; тонкая линия — шов
- плитка с подрезкой (размер — на цепочке)
- ось старта; стрелки — направление укладки
- сантехприбор: габарит, высота по практике
- короб инсталляции: плитка пола — до короба
- отметка чистого пола на полке выноски, м
- (А) обозначение стены А–Г (как на развёртках)

Ведомость плитки

Помещение, поверхность	Плитка, код	Формат	Шов	S, м²	Целых	Подр.	С запасом
Ванная комната, пол	керамогранит матовый R10, тон J484	600.8×600.8	2	5,57	6	14	22
Ванная комната, стены А–Г	керамогранит матовый, тон F497	600.8×600.8	2	21,66	23	67	100
Ванная комната, короб инсталляции	керамогранит матовый, тон F497	600.8×600.8	2	1,36	1	6	8
Коридор, пол	керамогранит матовый R10, тон V486	600.8×600.8	2	4,54	0	14	16
Прихожая-коридор, пол	керамогранит матовый R10, тон V486	600.8×600.8	2	7,80	9	16	28
Санузел, пол	керамогранит матовый R10, тон J484	600.8×600.8	2	1,31	0	6	7
Санузел, стены А–Г	керамогранит матовый, тон F497	600.8×600.8	2	9,44	6	44	56
Санузел, короб инсталляции	керамогранит матовый, тон F497	600.8×600.8	2	1,76	0	10	11
Кухня, фартук (ст. А)	аналог: керамогранит матовый, тон F497	600.8×600.8	2	1,11	1	3	5
Итого 600.8×600.8				**54,54**	**46**	**180**	**253**

Ведомость материалов

Материал	Класс, код	Норма расхода	Кол-во
Затирка	CG2WA аналог: Mapei Ultracolor 133	(a+b)/ab·шов·t·1,6	5,6 кг
Затирка	CG2WA	(a+b)/ab·шов·t·1,6	0,1 кг
Клей	C2 TE S1 аналог: Litokol K80 Eco	1,5 кг/м²·мм, слой 5	425 кг (17 меш.)
Клей	C2 TE S1	1,5 кг/м²·мм, слой 5	10 кг (1 меш.)
Гидроизоляция	обмазочная, 2 слоя: пол, стены по периметру и зоны замачивания	по ТУ	16,2 м²
Демпф. лента	по периметру пола из плитки		29,1 м


Примечания

1. Раскладка от чистовых размеров: стены санузлов теряют 10 + 5 + 9 = 24 мм на сторону (штукатурка, клей, плитка); подрезки — чистые, без шва.
2. Старт — от центра помещения (штрихпунктир, стрелки — направление укладки); размер старта — от чистовых стен Г и А.
3. Раскладка фартука «Кухня» — на листе «Раскладка плитки. Фартук кухни».
4. Количество: целые по раскладке + по одной на подрезку, запас 10 %; один артикул — одна партия и тон. Исключены поддон, короб, проёмы и места за коробом; S — по чистым граням: стены нетто = зона облицовки по ведомости отделки − место за коробом инсталляции 1,71 м² (плитку за коробом не кладут), короб — отдельной строкой.
5. Клей C2 TE S1 аналог: Litokol K80 Eco; C2 TE S1 (ГОСТ Р 56387-2018), затирка CG2WA аналог: Mapei Ultracolor 133; CG2WA; расход — по ТУ выбранной марки.
6. Гидроизоляция: пол и стены 200 мм от ЧП; над ванной — до 2100 и 300 мм за борт (см. развёртки); акт скрытых работ, пролив 24 ч.
7. Швы пола совмещены со швами стены А; по периметру — демпферная лента.
8. Отметка чистого пола −0,015, порог 15 мм; стык с соседним покрытием — по оси полотна двери.

					Проект: Четырёхкомнатная квартира			
	Лист	№ док.	Подпись	Дата	Раскладка плитки. Планы полов	Стадия	Лист	Листов
Дизайнер	Кырпан А.С.			05.10.26		П	34	111

выпуск 05.10.2026 · d0efc1af8a · стр. 34 из 111

Фрагмент 1. Кухня (пом. 6), фартук, стена А. 600×600, шов 2 мм, М 1:20

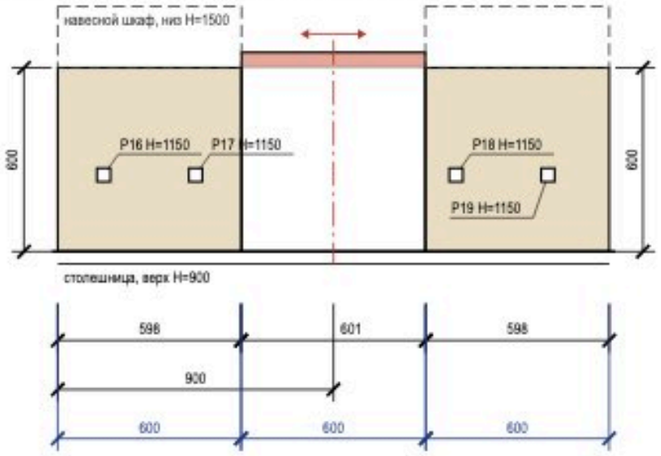

Условные обозначения

- плитка целая; тонкая линия — шов
- плитка с подрезкой (размер — на цепочке)
- ось старта; стрелки — направление укладки
- электроточка: марка и H — по листам ЭОМ
- столешница (верх)
- навесной шкаф над фартуком

Подсчёт плитки

Поверхность	Формат	S, м²	Целых	Подр.	С запасом
Кухня, фартук (ст. А)	600×600	1,11	1	3	5

Сдвиг розеток фартука под раскладку

Точка (ЭОМ)	Проект: от угла / H	Под раскладку: от угла / H	Сдвиг, мм
P16	150 / 1150	297 / 1200	+147 от шва; H +50 ось ряда
P17	450 / 1150	599 / 1200	+149 на шов; H +50 ось ряда
P18	1300 / 1150	1201 / 1200	−99 на шов; H +50 ось ряда
P19	1600 / 1150	1503 / 1200	−97 от шва; H +50 ось ряда

Примечания

1. Фартук, Кухня: 600×600 горизонтально, шов 2 мм; зоны 600 мм — 900…1500, 600 мм — 900…1550, 600 мм — 900…1500 (от столешницы до низа навесного шкафа, без шкафа — 650 мм). Старт от центра участка, подрезки 598 мм. Площадь 1,11 м² — как в ведомости отделки.
2. Фартук — после монтажа столешницы, низ на 2–3 мм выше неё, шов со столешницей — санитарный герметик; навесные шкафы — после фартука. Торцы у пенала и стены — профиль или запил 45°.
3. Фартук, Кухня: в зоне до отм. 1550 верхний ряд подрезан 47 мм — меньше 1/3 плитки; полоса прикрыта корпусом навесного модуля и на виду не остаётся. Раскладкой не снимается: убрать подрезку можно, только выровняв низ этого модуля с соседними (1500 мм) — решение мебельщика.
4. Розетки из таблицы переносятся до черновой электрики: по высоте — на ось ряда плитки, от вертикального шва крупной плитки — не ближе 60 мм. Привязка — от левого края фартука на развёртке.
5. Клей, затирка и итог по форматам — в ведомостях листа «Раскладка плитки. Планы полов».

					Проект: Четырёхкомнатная квартира
	Лист	№ док.	Подпись	Дата	Раскладка плитки. Фартук кухни
Дизайнер	Кырпан А.С.			05.10.26	

Стадия	Лист	Листов
П	35	111

выпуск 05.10.2026 · d0efc1af8a · стр. 35 из 111



					Проект: Четырёхкомнатная квартира			
	Лист	№ док.	Подпись	Дата	Визуализация. Вид сверху	Стадия	Лист	Листов
Дизайнер	Кырпан А.С.			05.10.26		П	36	111

выпуск 05.10.2026 № d0efc1af8a · стр. 36 из 111



					Проект: Четырёхкомнатная квартира	
	Лист	№ док.	Подпись	Дата		
Дизайнер	Кырпан А.С.			05.10.26	Визуализация: Зал	Стадия: П; Лист: 37; Листов: 111

выпуск 05.10.2026 № d0efc1af8a · стр. 37 из 111



					Проект: Четырёхкомнатная квартира
	Лист	№ док.	Подпись	Дата	Визуализация: Зал
Дизайнер	Кырпан А.С.			05.10.26	

Стадия	Лист	Листов
П	38	111

выпуск 05.10.2026 · d0efc1af8a · стр. 38 из 111



					Проект: Четырёхкомнатная квартира	
	Лист	№ док.	Подпись	Дата		
Дизайнер	Кырпан А.С.			05.10.26	Визуализация: Зал	Стадия / Лист / Листов
						П / 39 / 111

выпуск 05.10.2026 · d0efc1af8a · стр. 39 из 111



					Проект: Четырёхкомнатная квартира	
	Лист	№ док.	Подпись	Дата	Визуализация: Зал	Стадия / Лист / Листов
Дизайнер	Кырпан А.С.			05.10.26		П / 40 / 111

выпуск 05.10.2026 № d0efc1af8a · стр. 40 из 111

Развёртка стены А


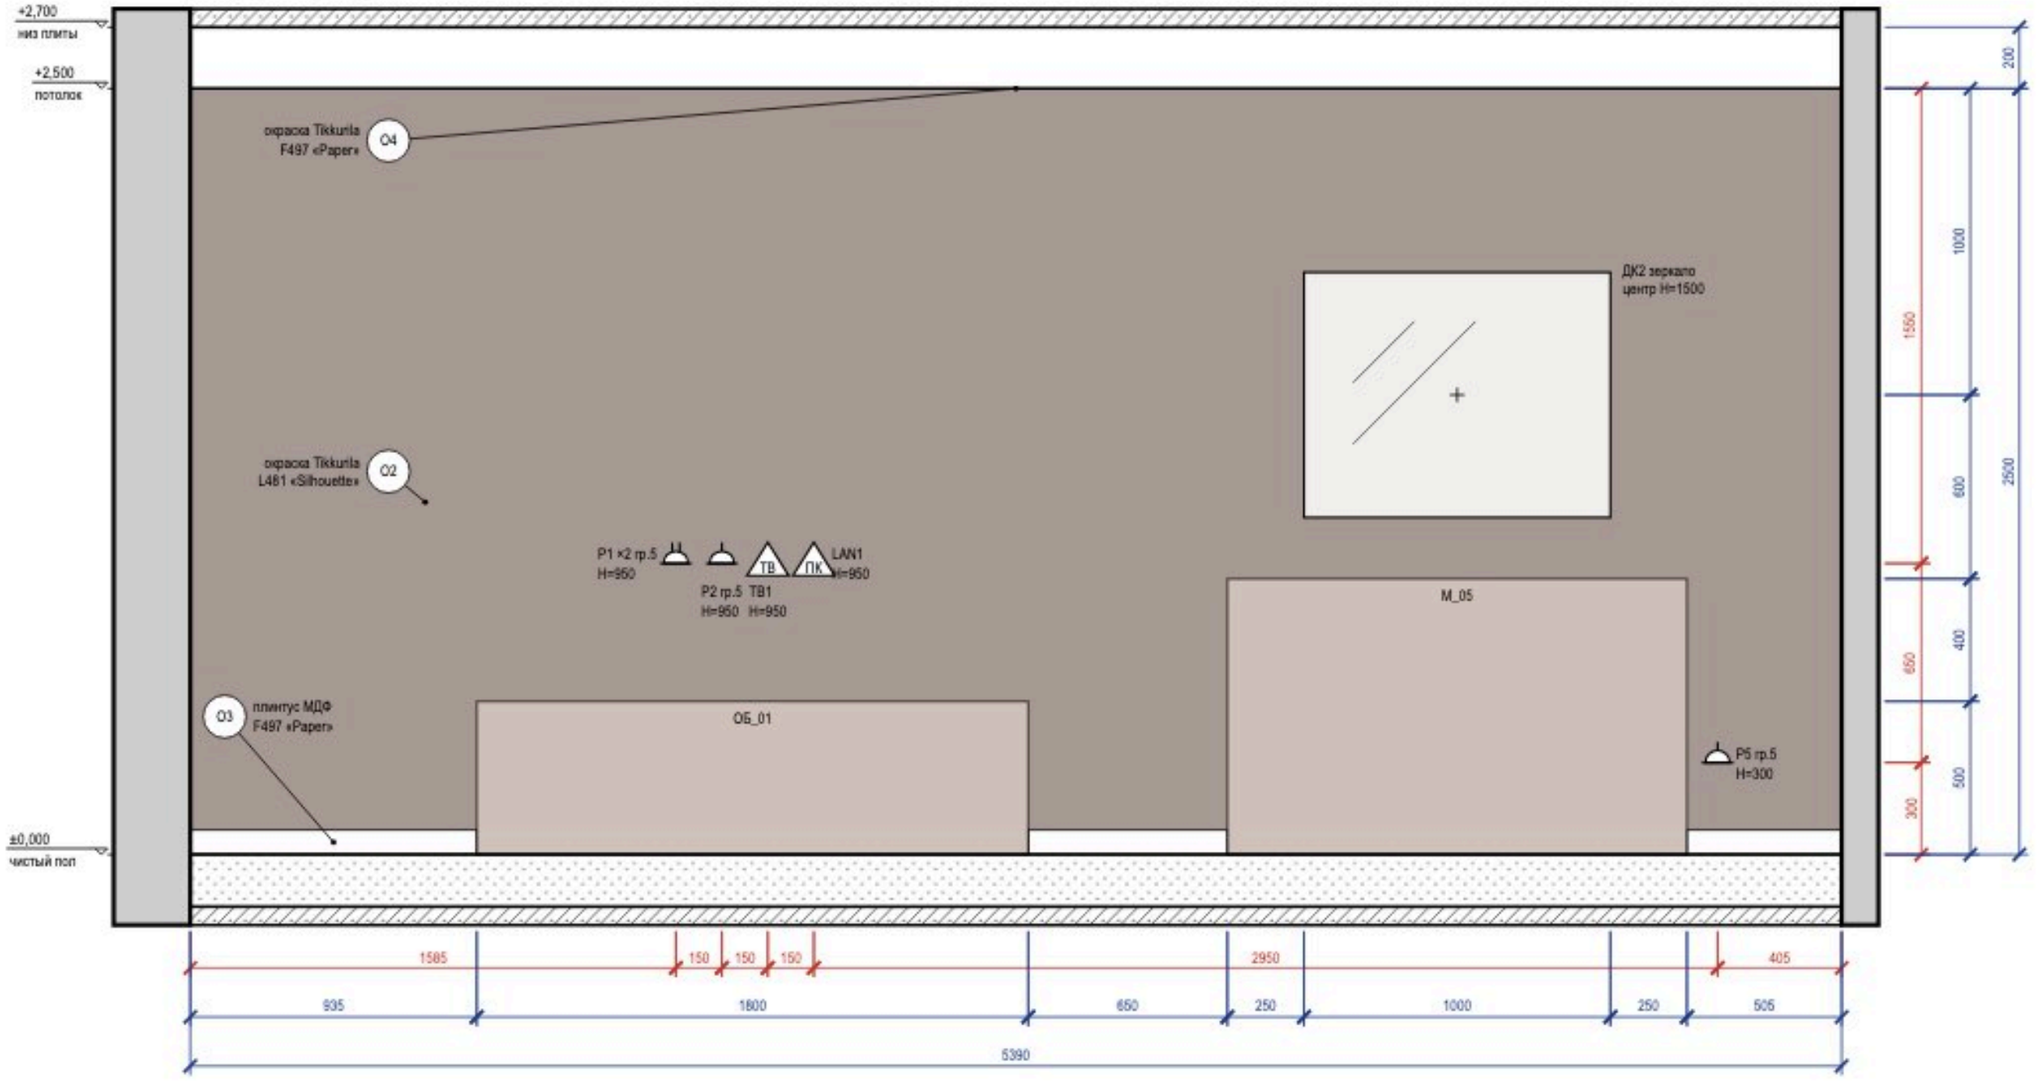



Схема развёрток (М 1:100)

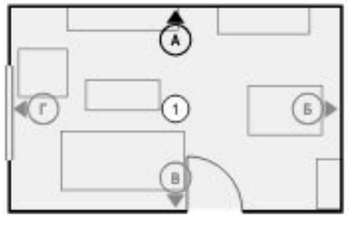

Ведомость отделки (на листе)

Марка	Поверхность	Материал, изделие	Цвет, код	Кол.
О2	акцентная стена	краска, Tikkurila Optiva 5 Matt, аналог: интерьерная краска, класс 2 по EN 13300, глубокоматовая/матовая, база С, матовая, подготовка К3	Tikkurila L481 «Silhouette»	13,5 м²
О3	плинтус	плинтус МДФ, h 80 мм, аналог: плинтус МДФ под окраску 80×16 мм, полуглянцевая	Tikkurila F497 «Paper»	2,1 м
О4	потолок	краска, Tikkurila Anti-Reflex 2, глубокоматовая, подготовка Q3	Tikkurila F497 «Paper»	18,2 м²

Визуализация этой стены — лист 37

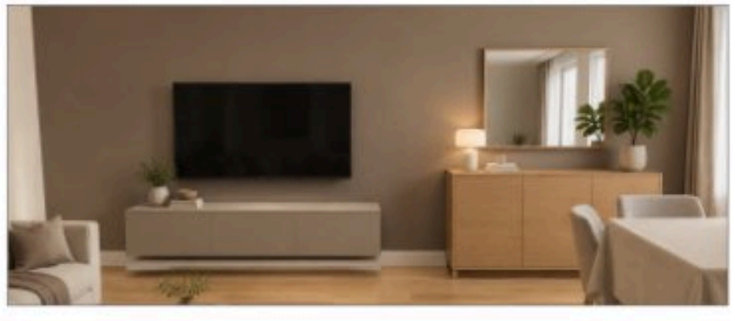

Примечания

1. Размеры — в мм от чистовых поверхностей стен; условные обозначения и общие указания — лист 2.
2. Картины и зеркала крепить к основанию по паспорту изделия (закладные и анкеры — в перечне скрытых работ); «крест — ось центра предмета.
3. Потолок на развёртках — по нижнему уровню У1; другие уровни потолка помещения: У2 +2,600.

					Проект: Четырёхкомнатная квартира
	Лист	№ док.	Подпись	Дата	
Дизайнер	Кырпан А.С.			05.10.26	Развёртка стены А. Зал (пом. 1)

Стадия	Лист	Листов
П	41	111

выпуск 05.10.2026 · d0efc1af8a · стр. 41 из 111

Развёртка стены Б

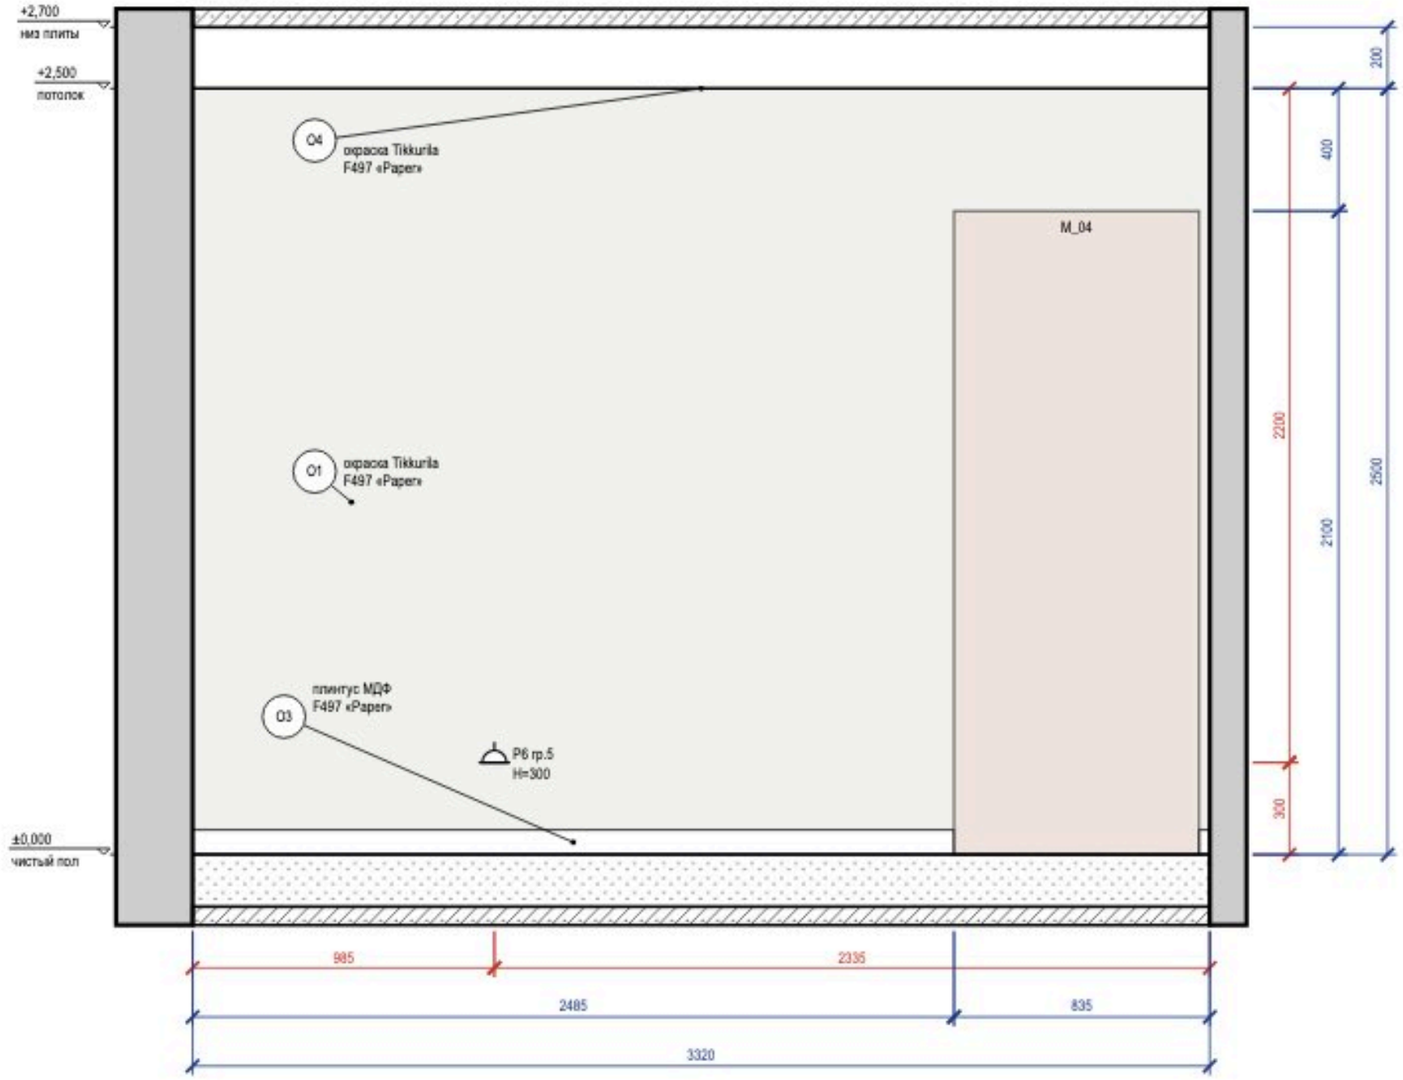



Схема развёрток (М 1:100)



Ведомость отделки (на листе)

Марка	Поверхность	Материал, изделие	Цвет, код	Кол.
О1	стены	окраска, Tikkurila Optiva 5 Matt, матовая, подготовка К3	Tikkurila F497 «Paper»	8,3 м²
О3	плинтус	плинтус МДФ, h 80 мм, аналог: плинтус МДФ под окраску 80×16 мм, полуглянцевая	Tikkurila F497 «Paper»	2,5 м
О4	потолок	окраска, Tikkurila Anti-Reflex 2, глубокоматовая, подготовка Q3	Tikkurila F497 «Paper»	18,2 м²

Визуализация этой стены — лист 38

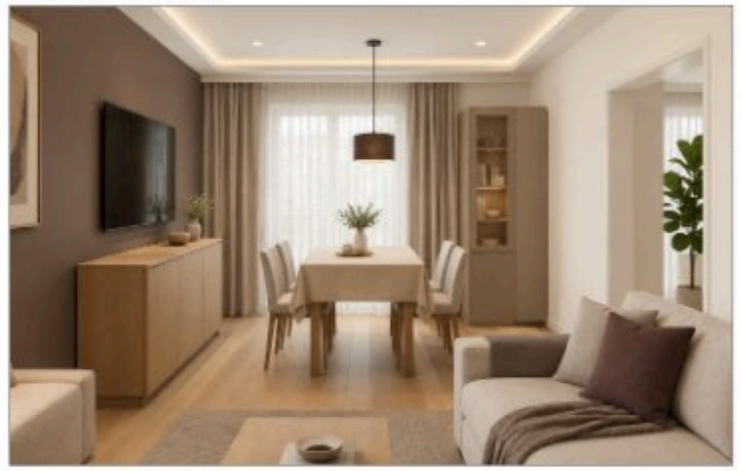

Примечания

1. Размеры — в мм от чистовых поверхностей стен; условные обозначения и общие указания — лист 2.
2. Потолок на развёртках — по нижнему уровню У1; другие уровни потолка помещения: У2 +2,600.

	Лист	№ док.	Подпись	Дата	Проект: Четырёхкомнатная квартира			
Дизайнер	Кырпан А.С.			05.10.26	Развёртка стены Б. Зал (пом. 1)	Стадия	Лист	Листов
						П	42	111

выпуск 05.10.2026 · d0efc1af8a · стр. 42 из 111

Развёртка стены В


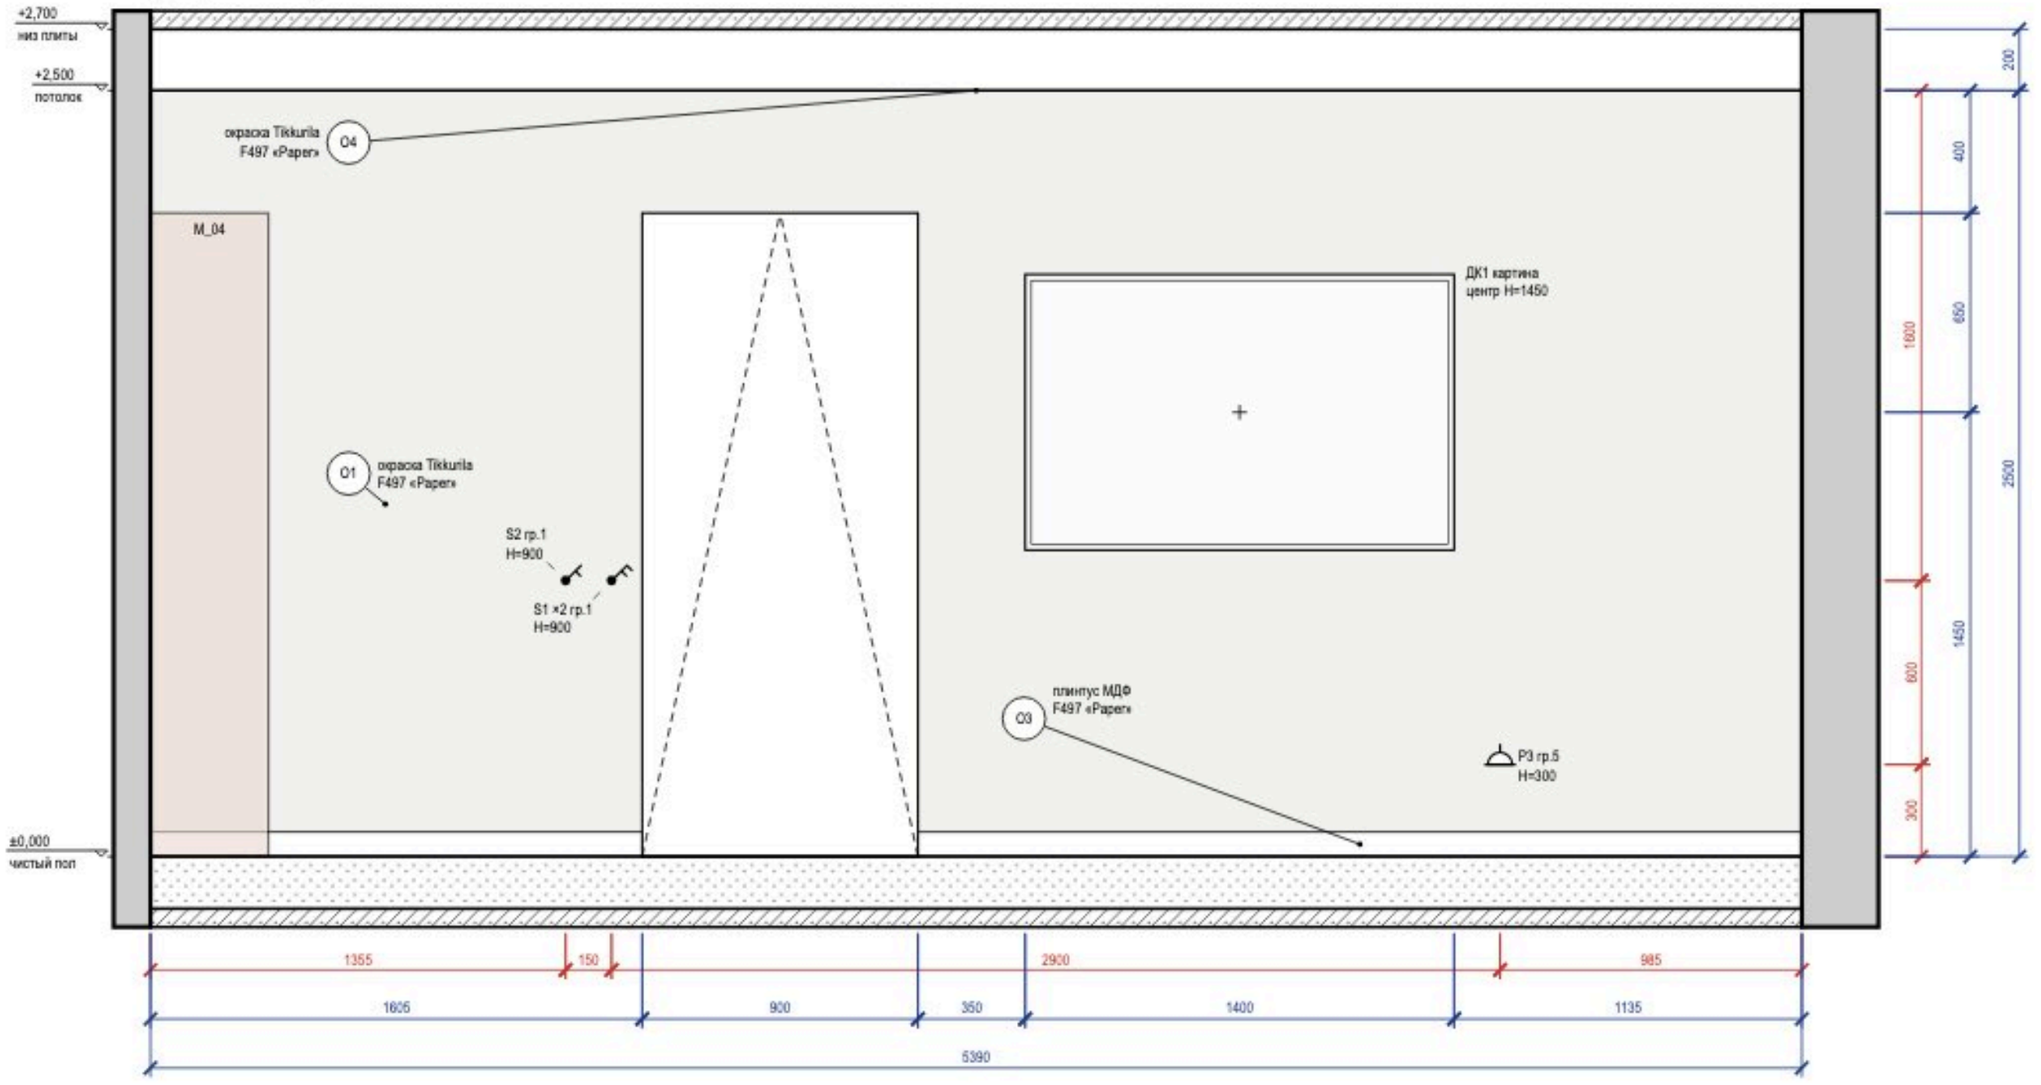



Схема развёрток (М 1:100)

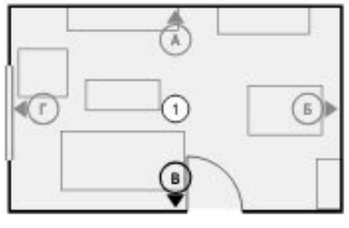

Ведомость отделки (на листе)

Марка	Поверхность	Материал, изделие	Цвет, код	Кол.
O1	стены	окраска, Tikkurila Optiva 5 Matt, матовая, подготовка К3	Tikkurila F497 «Paper»	11,6 м²
O3	плинтус	плинтус МДФ, h 80 мм, аналог: плинтус МДФ под окраску 80×16 мм, полуглянцевая	Tikkurila F497 «Paper»	4,5 м
O4	потолок	окраска, Tikkurila Anti-Reflex 2, глубокоматовая, подготовка Q3	Tikkurila F497 «Paper»	18,2 м²

Визуализация этой стены — лист 39

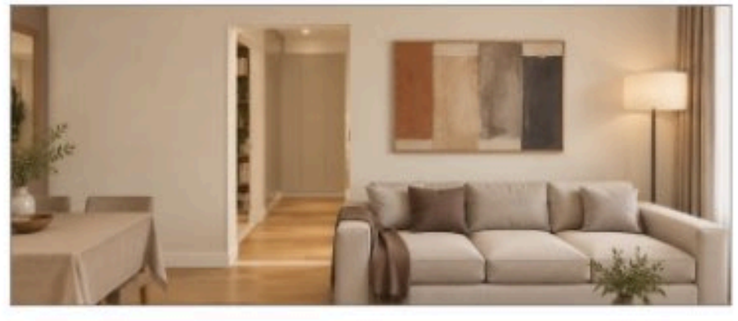

Примечания

1. Размеры — в мм от чистовых поверхностей стен; условные обозначения и общие указания — лист 2.
2. Картины и зеркала крепить к основанию по паспорту изделия (закладные и анкеры — в перечне скрытых работ); «крест — ось центра предмета.
3. Потолок на развёртках — по нижнему уровню У1; другие уровни потолка помещения: У2 +2,600.

					Проект: Четырёхкомнатная квартира
	Лист	№ док.	Подпись	Дата	
Дизайнер	Кырпан А.С.			05.10.26	Развёртка стены В. Зал (пом. 1)
					Стадия: П; Лист: 43; Листов: 111

выпуск 05.10.2026 · d0efc1af8a · стр. 43 из 111

Развёртка стены Г

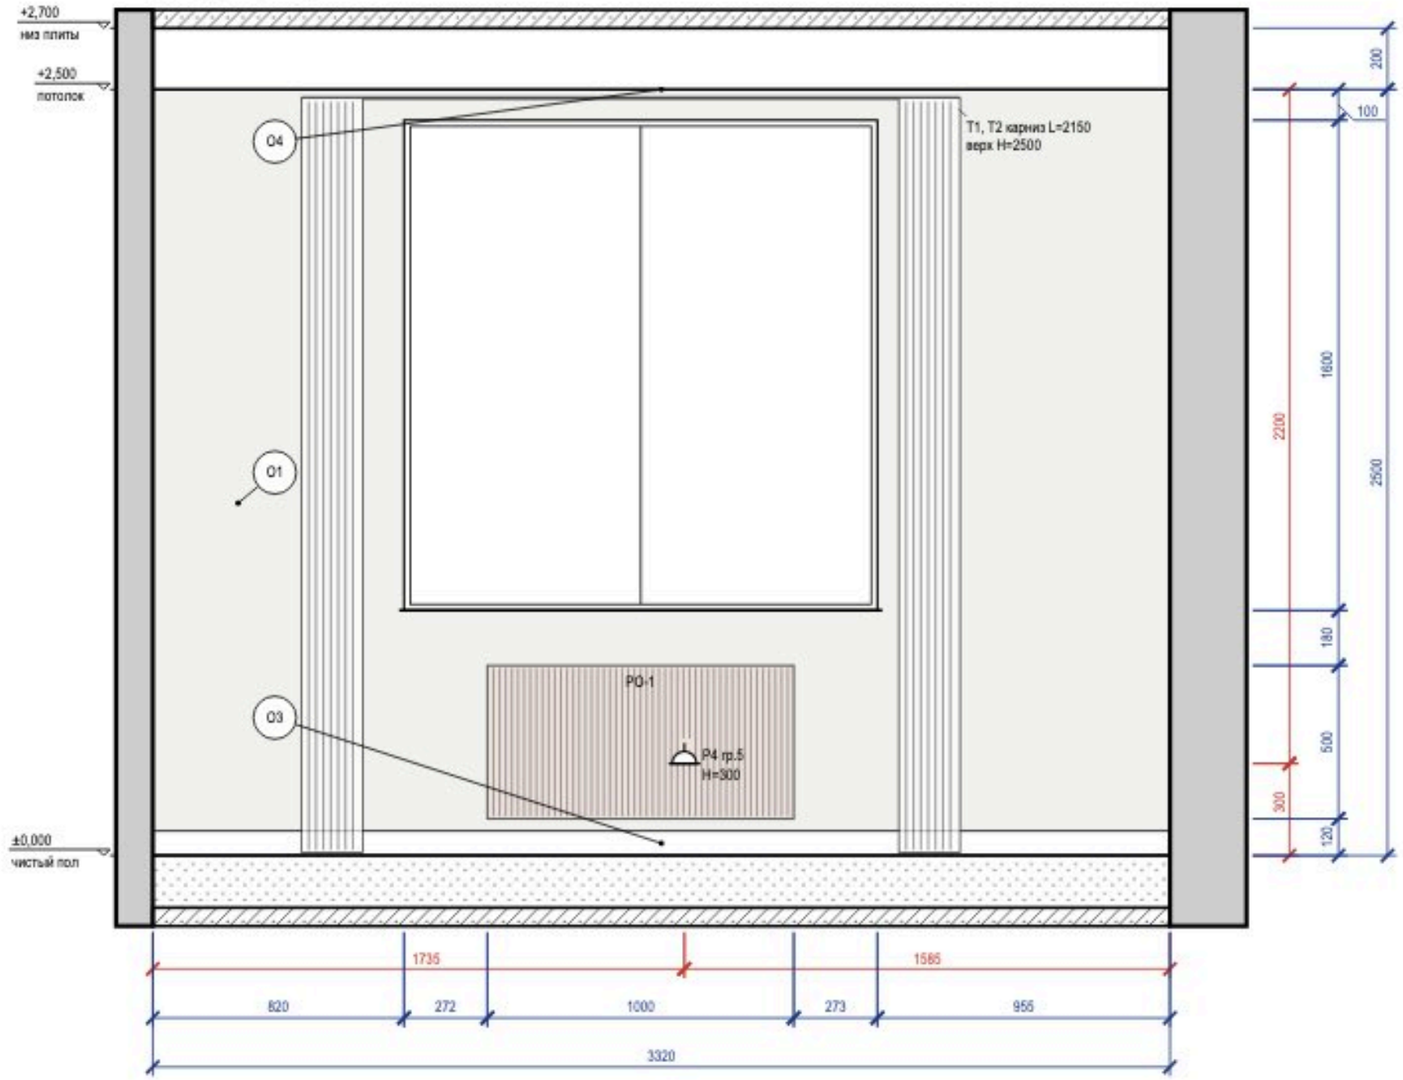


Схема развёрток (М 1:100)



Ведомость отделки (на листе)

Марка	Поверхность	Материал, изделие	Цвет, код	Кол.
О1	стены	окраска, Tikkurila Optiva 5 Matt, матовая, подготовка К3	Tikkurila F497 «Paper»	5,6 м²
О3	плинтус	плинтус МДФ, h 80 мм, аналог: плинтус МДФ под окраску 80×16 мм, полуглянцевая	Tikkurila F497 «Paper»	3,3 м
О4	потолок	окраска, Tikkurila Anti-Reflex 2, глубокоматовая, подготовка Q3	Tikkurila F497 «Paper»	18,2 м²

Визуализация этой стены — лист 40



Примечания

1. Размеры — в мм от чистовых поверхностей стен; условные обозначения и общие указания — лист 2.
2. Карнизы (шины) — по ведомости текстиля декоратора; длина L и верх H — по развёртке, крепление — до окраски потолка.
3. Потолок на развёртках — по нижнему уровню У1; другие уровни потолка помещения: У2 +2,600.
4. Линии узора (швы плитки, складки штор, рёбра радиаторов) прерываются у знаков и выносок — просвет между линиями не менее 0,7 мм.

					Проект: Четырёхкомнатная квартира			
	Лист	№ док.	Подпись	Дата	Развёртка стены Г. Зал (пом. 1)	Стадия	Лист	Листов
Дизайнер	Кырпан А.С.			05.10.26		П	44	111


выпуск 05.10.2026 · d0efc1af8a · стр. 44 из 111



					Проект: Четырёхкомнатная квартира	
	Лист	№ док.	Подпись	Дата	Визуализация: Ванная комната	Стадия / Лист / Листов
Дизайнер	Кырпан А.С.			05.10.26		П / 45 / 111

выпуск 05.10.2026 · d0efc1af8a · стр. 45 из 111

Развёртка стены А

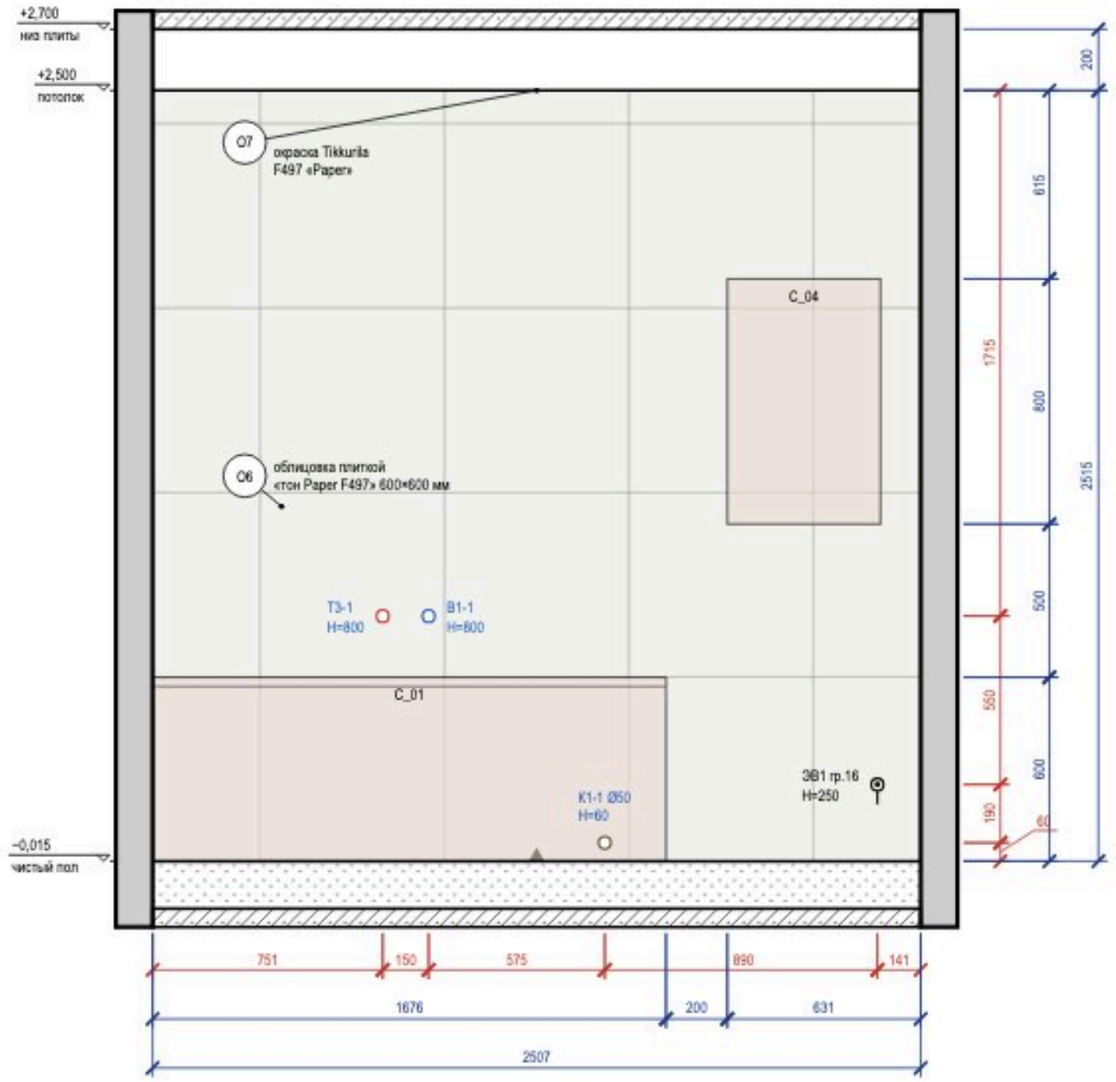

Развёртка стены Б

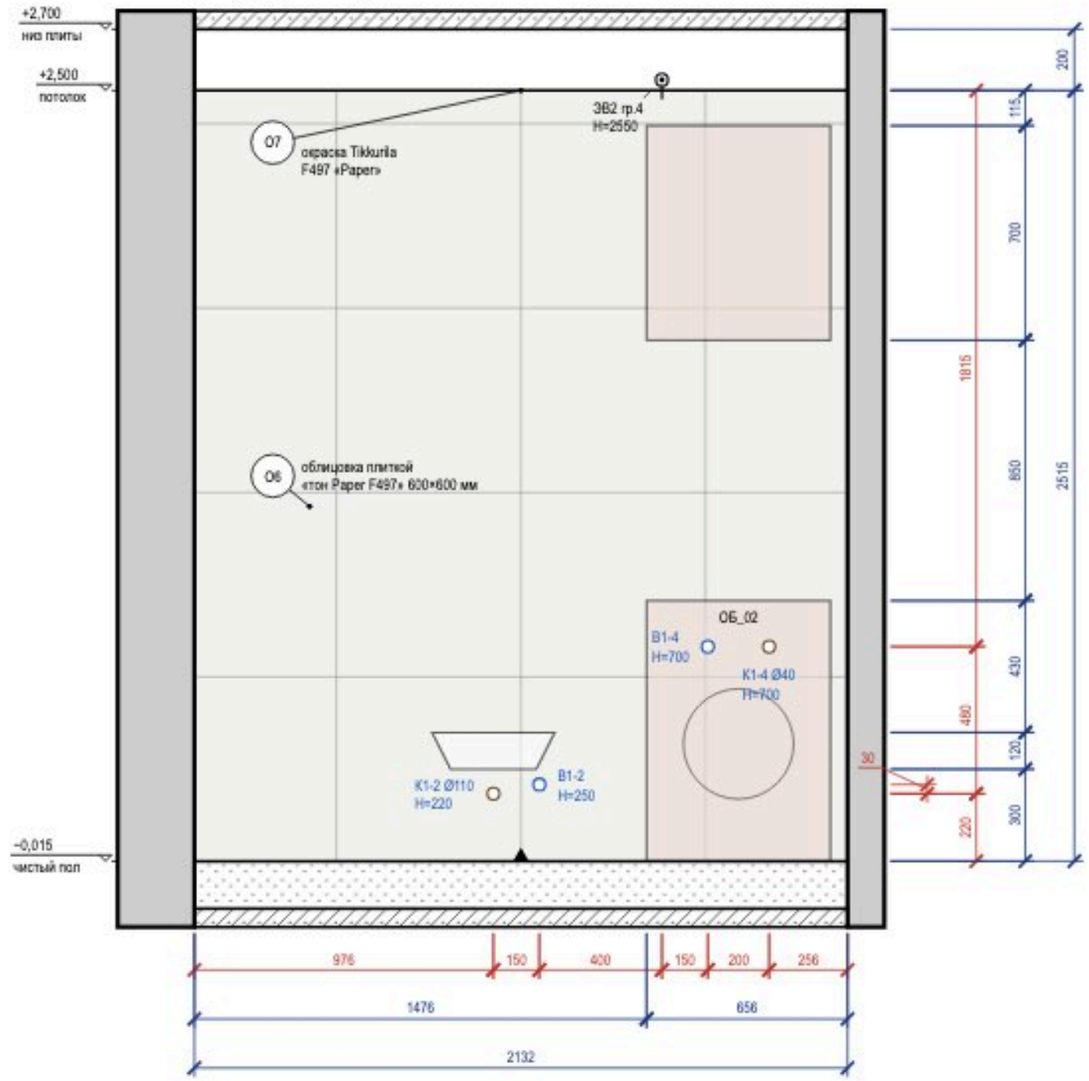



Схема развёрток (М 1:100)



Ведомость отделки (на листе)

Марка	Поверхность	Материал, изделие	Цвет, код	Кол.
О6	стены	облицовка плиткой, 600×600×9 мм, аналог: керамогранит матовый, тон F497, затирка CG2WA	#F1F1EC «тон Paper F497»	11,7 м²
О7	потолок	окраска, Tikkurila Luja 7, матовая, подготовка Q3	Tikkurila F497 «Paper»	5,6 м²

Визуализация этой стены — лист 45

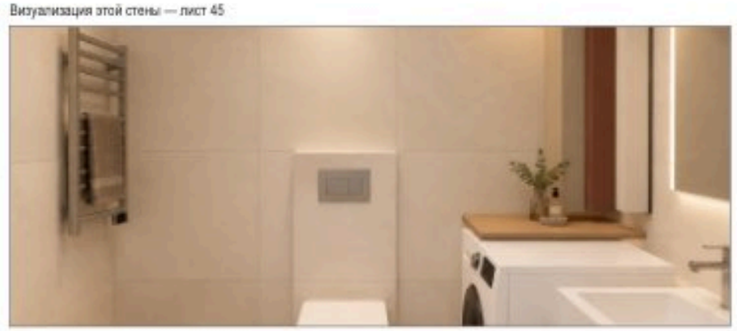

Примечания


1. Размеры — в мм от чистовых поверхностей стен; условные обозначения и общие указания — лист 2.
2. Схема мебели, приборов и декора не является технической документацией для производства мебели; габариты — по паспортам изделий.
3. Облицовка — по сетке швов 2 мм, раскладка от оси стены (треугольник у пола); подрезки — по листу раскладки плитки.
4. Гидроизоляция в 2 слоя, заход на стены 200 мм, в зоне душа — 2100 мм — до облицовки, с актом скрытых работ и тестом проливом (узел — на листе узлов).

					Проект: Четырёхкомнатная квартира
	Лист	№ док.	Подпись	Дата	Развёртки стен А, Б. Ванная комната (пом. 2)
Дизайнер	Кырпан А.С.			05.10.26	

Стадия	Лист	Листов
П	46	111

выпуск 05.10.2026 · d0efc1af8a · стр. 46 из 111

Развёртка стены В

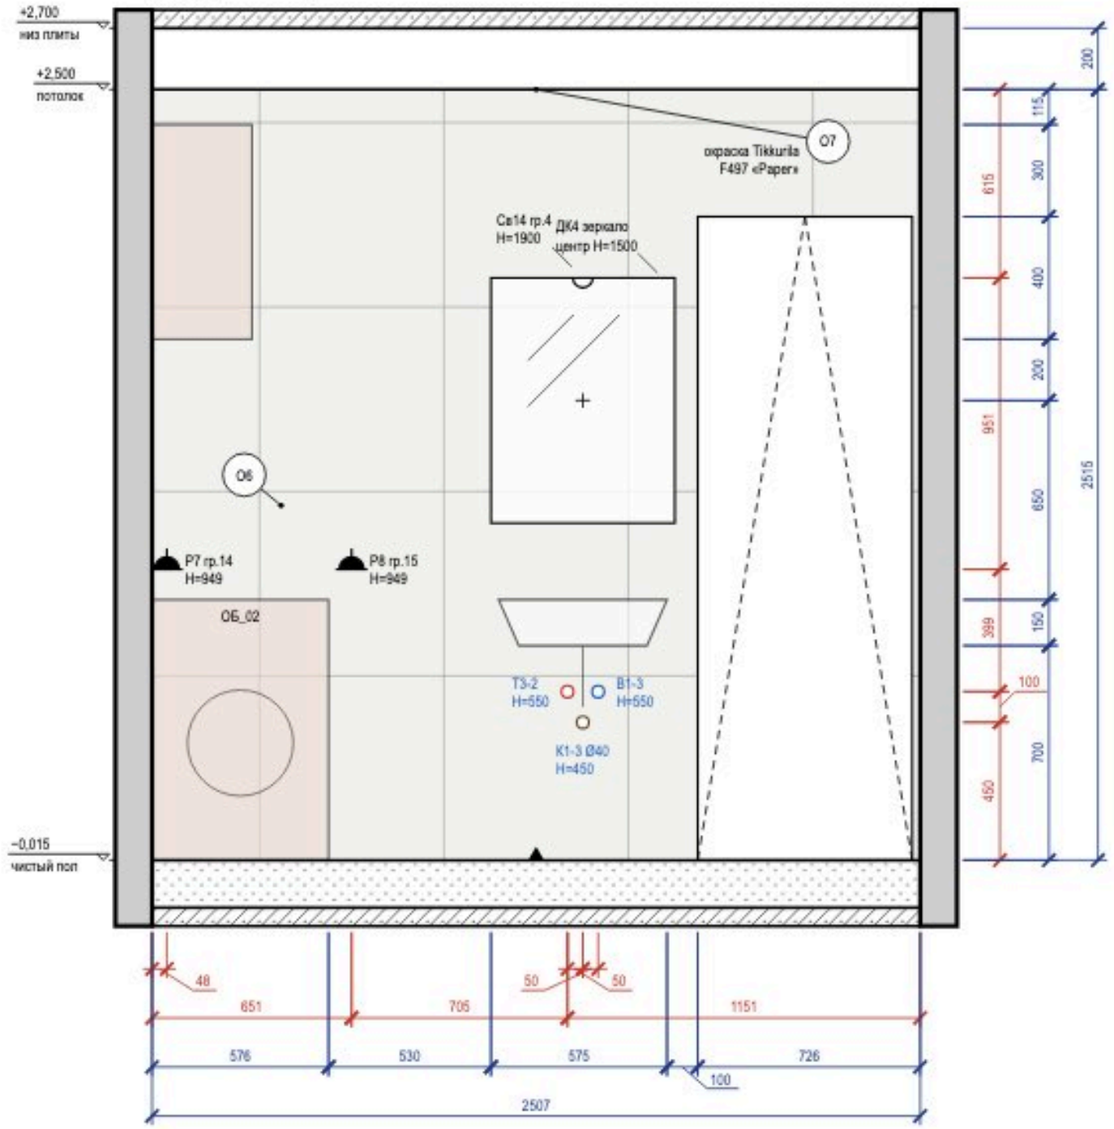

Развёртка стены Г

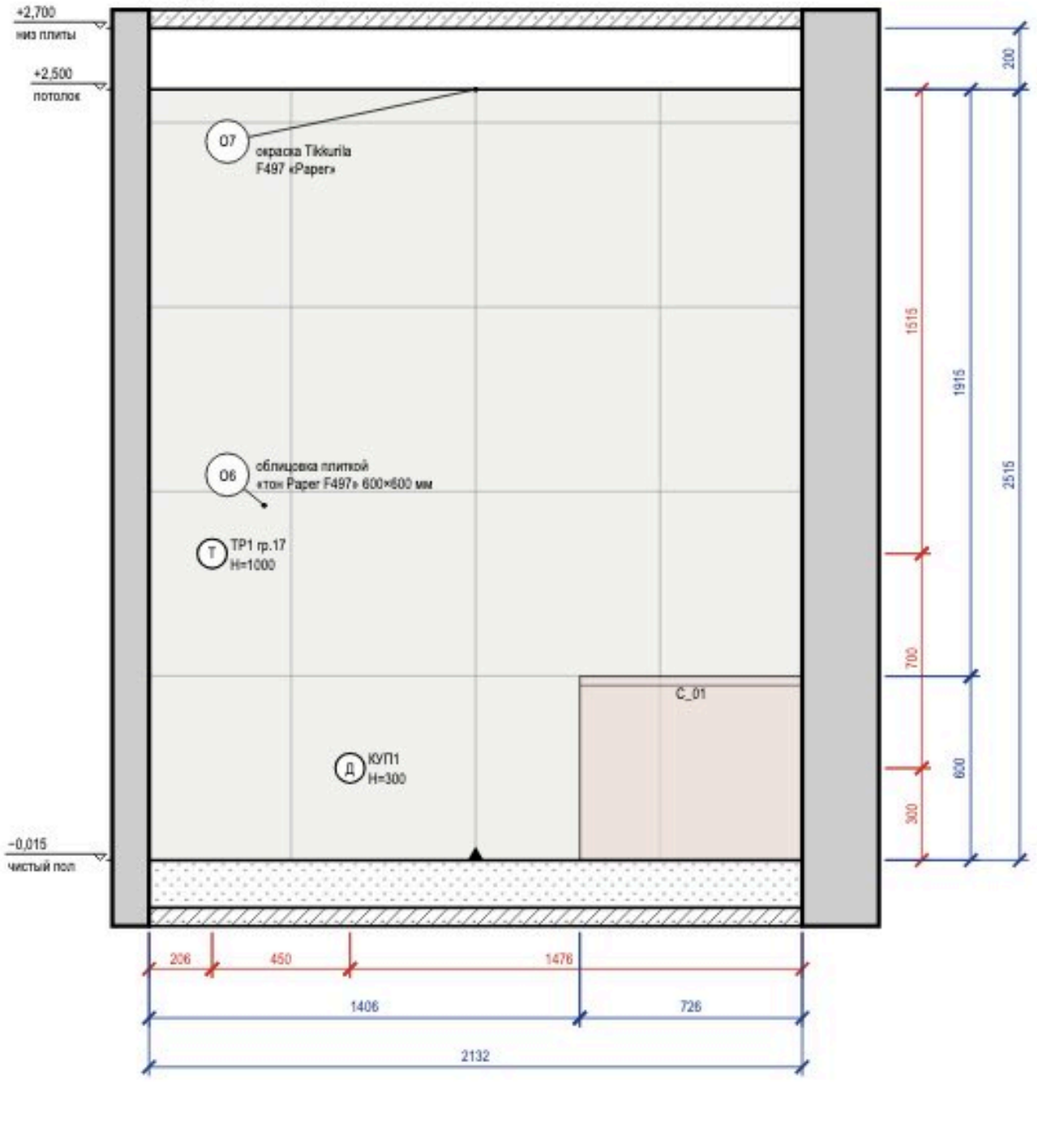


Схема развёрток (М 1:100)



Ведомость отделки (на листе)

Марка	Поверхность	Материал, изделие	Цвет, код	Кол.
О6	стены	облицовка плиткой, 600×600×9 мм, аналог: керамогранит матовый, тон F497, затирка CG2WA	#F1F1EC «тон Paper F497»	10,2 м²
О7	потолок	окраска, Tikkurila Luja 7, матовая, подготовка Q3	Tikkurila F497 «Paper»	5,6 м²

Примечания

1. Размеры — в мм от чистовых поверхностей стен; условные обозначения и общие указания — лист 2.
2. Схема мебели, приборов и декора не является технической документацией для производства мебели; габариты — по паспортам изделий.
3. Облицовка — по сетке швов 2 мм, раскладка от оси стены (треугольник у пола); подрезки — по листу раскладки плитки.
4. Гидроизоляция в 2 слоя, заход на стены 200 мм, в зоне душа — 2100 мм — до облицовки, с актом скрытых работ и тестом проливом (узел — на листе узлов).
5. Картины и зеркала крепить к основанию по паспорту изделия (закладные и анкеры — в перечне скрытых работ); крест — ось центра предмета.

					Проект: Четырёхкомнатная квартира
	Лист	№ док.	Подпись	Дата	Развёртки стен В, Г. Ванная комната (пом. 2)
Дизайнер	Кырпан А.С.			05.10.26	

Стадия	Лист	Листов
П	47	111


выпуск 05.10.2026 · d0efc1af8a · стр. 47 из 111




					Проект: Четырёхкомнатная квартира	
	Лист	№ док.	Подпись	Дата		
Дизайнер	Кырпан А.С.			05.10.26	Визуализация: Тёмная комната	Стадия / Лист / Листов
						П / 48 / 111

выпуск 05.10.2026 № d0efc1af8a · стр. 48 из 111

Развёртка стены А

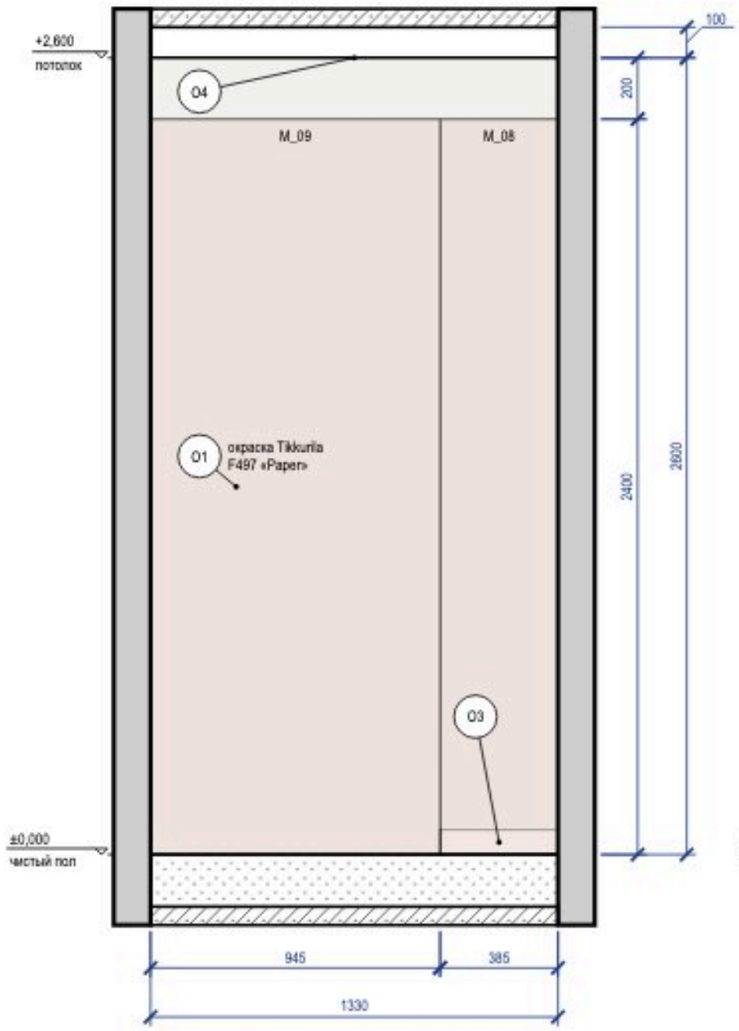


Развёртка стены Б

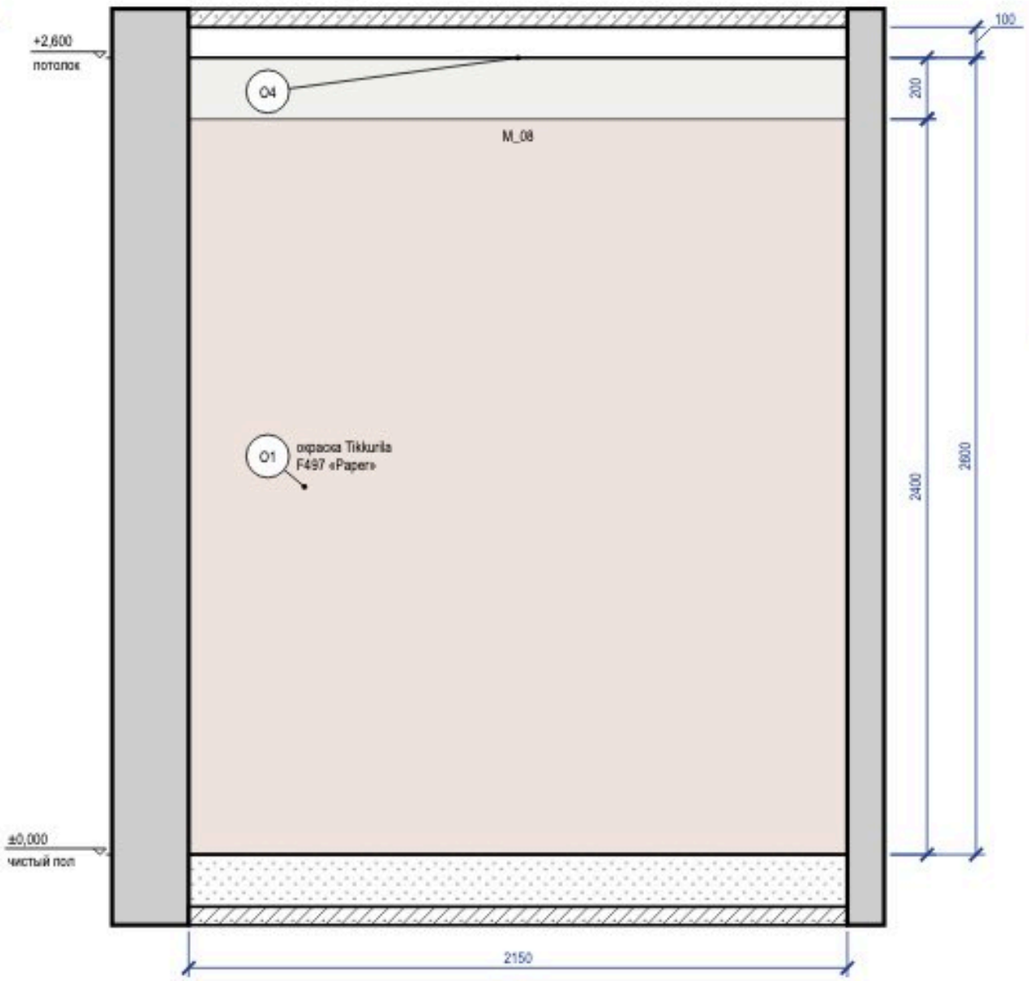

Визуализация этой стены — лист 48



Схема развёрток (М 1:100)

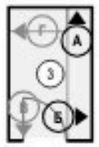

Ведомость отделки (на листе)

Марка	Поверхность	Материал, изделие	Цвет, код	Кол.
O1	стены	окраска, Tikkurila Optiva 5 Matt, матовая, подготовка К3	Tikkurila F497 «Paper»	9 м²
O3	плинтус	плинтус МДФ, h 80 мм, аналог: плинтус МДФ под окраску 80×16 мм, полуглянцевая	Tikkurila F497 «Paper»	0,4 м
O4	потолок	окраска, Tikkurila Anti-Reflex 2, глубокоматовая, подготовка Q3	Tikkurila F497 «Paper»	3 м²

Примечания


1. Размеры — в мм от чистовых поверхностей стен; условные обозначения и общие указания — лист 2.

	Лист	№ док.	Подпись	Дата	Проект: Четырёхкомнатная квартира
Дизайнер	Кырпан А.С.			05.10.26	Развёртки стен А, Б. Тёмная комната (пом. 3)

Стадия	Лист	Листов
П	49	111

выпуск 05.10.2026 · d0efc1af8a · стр. 49 из 111

Развёртка стены В

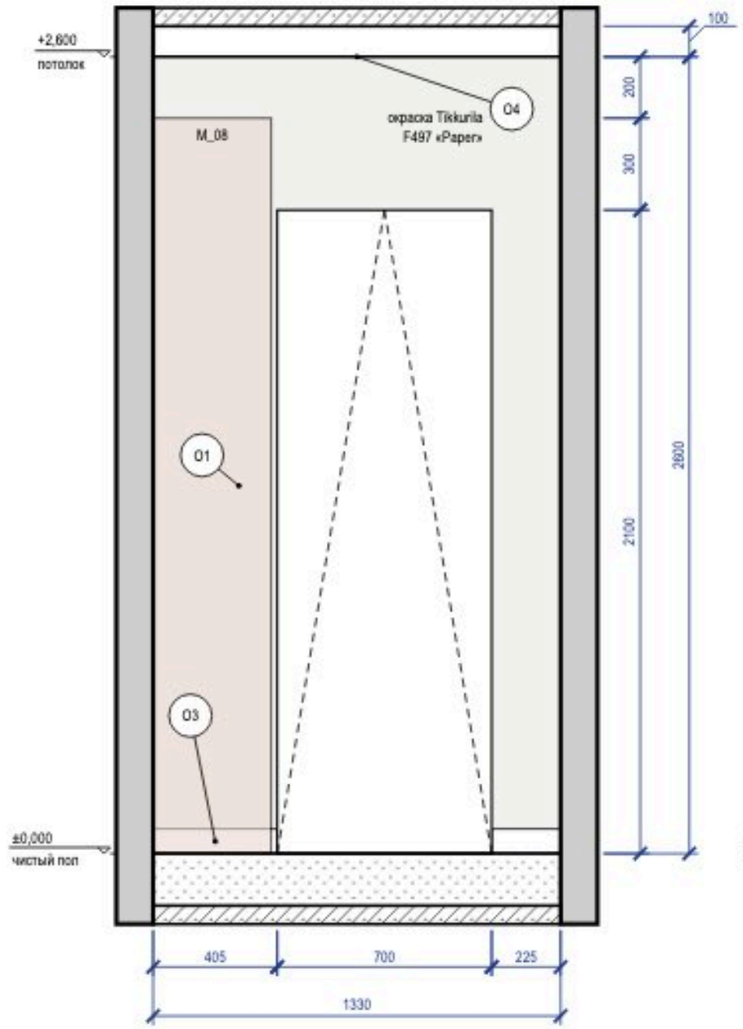

Развёртка стены Г


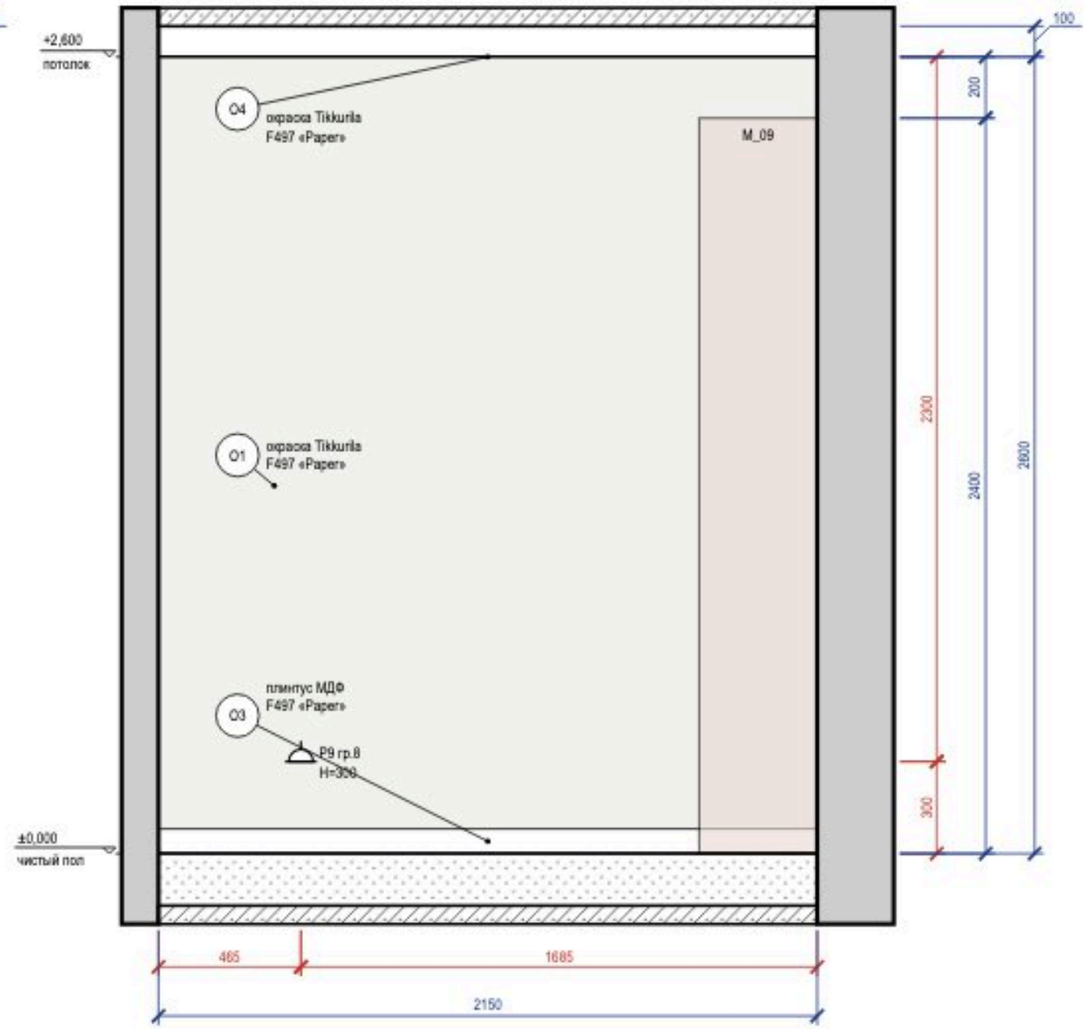


Схема развёрток (М 1:100)

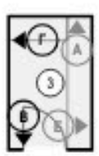

Ведомость отделки (на листе)

Марка	Поверхность	Материал, изделие	Цвет, код	Кол.
O1	стены	окраска, Tikkurila Optiva 5 Matt, матовая, подготовка К3	Tikkurila F497 «Paper»	7,6 м²
O3	плинтус	плинтус МДФ, h 80 мм, аналог: плинтус МДФ под окраску 80×16 мм, полуглянцевая	Tikkurila F497 «Paper»	2,8 м
O4	потолок	окраска, Tikkurila Anti-Reflex 2, глубокоматовая, подготовка Q3	Tikkurila F497 «Paper»	3 м²

Примечания

1. Размеры — в мм от чистовых поверхностей стен; условные обозначения и общие указания — лист 2.

					Проект: Четырёхкомнатная квартира
	Лист	№ док.	Подпись	Дата	Развёртки стен В, Г. Тёмная комната (пом. 3)
Дизайнер	Кырпан А.С.			05.10.26	

Стадия	Лист	Листов
П	50	111

выпуск 05.10.2026 № d0efc1af8a · стр. 50 из 111



					Проект: Четырёхкомнатная квартира
	Лист	№ док.	Подпись	Дата	
Дизайнер	Кырпан А.С.			05.10.26	Визуализация: Детская 1

Стадия	Лист	Листов
П	51	111

выпуск 05.10.2026 № d0efc1af8a · стр. 51 из 111



					Проект: Четырёхкомнатная квартира	
	Лист	№ док.	Подпись	Дата		
Дизайнер	Кырпан А.С.			05.10.26	Визуализация: Детская 1	Стадия: П; Лист: 52; Листов: 111

выпуск 05.10.2026 · d0efc1af8a · стр. 52 из 111

Развёртка стены А


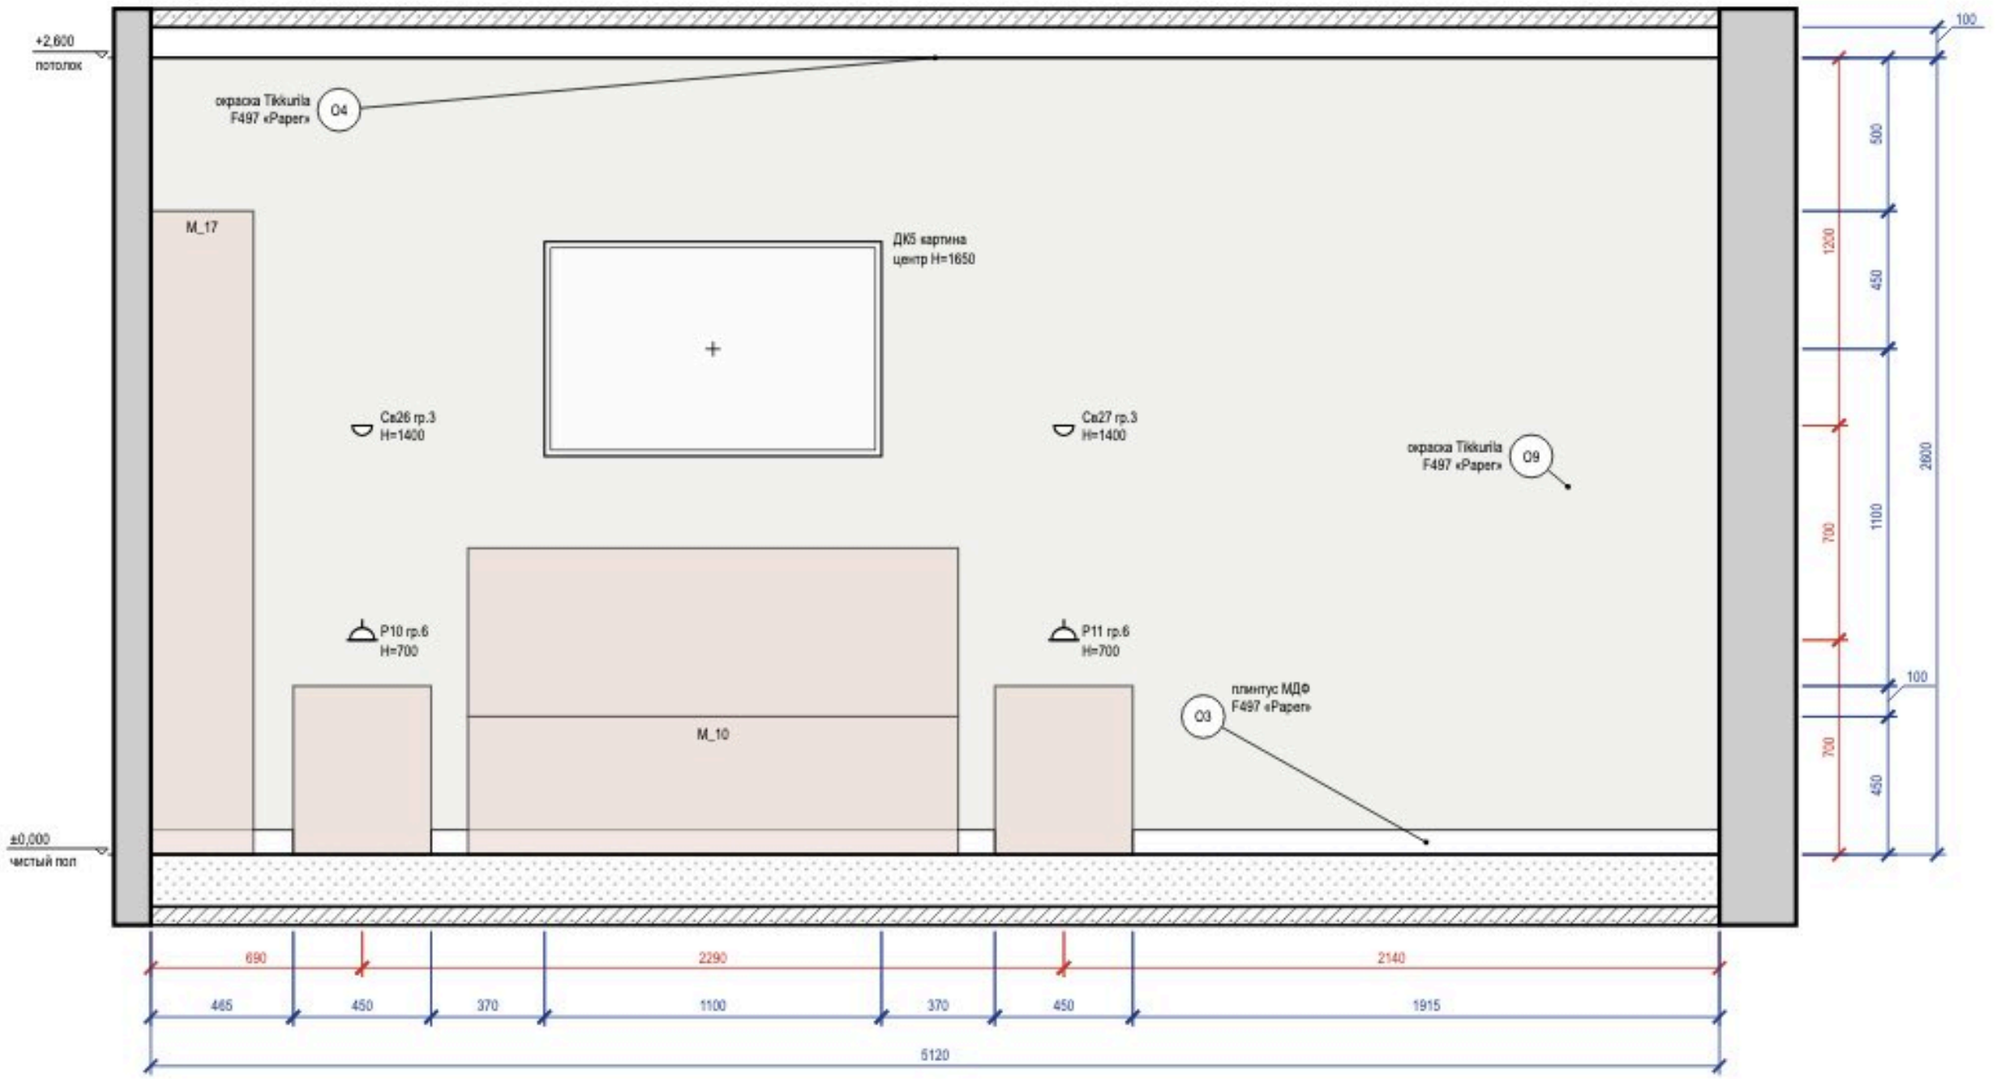


Схема развёрток (М 1:100)

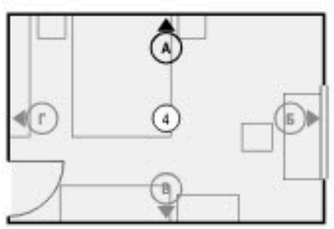

Ведомость отделки (на листе)

Марка	Поверхность	Материал, изделие	Цвет, код	Кол.
О3	плинтус	плинтус МДФ, h 80 мм, аналог: плинтус МДФ под окраску 80×16 мм, полуглянцевая	Tikkurila F497 «Paper»	4,2 м
О4	потолок	окраска, Tikkurila Anti-Reflex 2, глубокоматовая, подготовка О3	Tikkurila F497 «Paper»	17,5 м²
О9	стены	окраска, Tikkurila Joker, шелковисто-матовая, подготовка К3	Tikkurila F497 «Paper»	13,3 м²

Примечания

1. Размеры — в мм от чистовых поверхностей стен; условные обозначения и общие указания — лист 2.
2. Картины и зеркала крепить к основанию по паспорту изделия (закладные и анкеры — в перечне скрытых работ); крест — ось центра предмета.

					Проект: Четырёхкомнатная квартира
	Лист	№ док.	Подпись	Дата	Развёртка стены А. Детская 1 (пом. 4)
Дизайнер	Кырпан А.С.			05.10.26	

Стадия	Лист	Листов
П	53	111

выпуск 05.10.2026 · d0efc1af8a · стр. 53 из 111

Развёртка стены Б


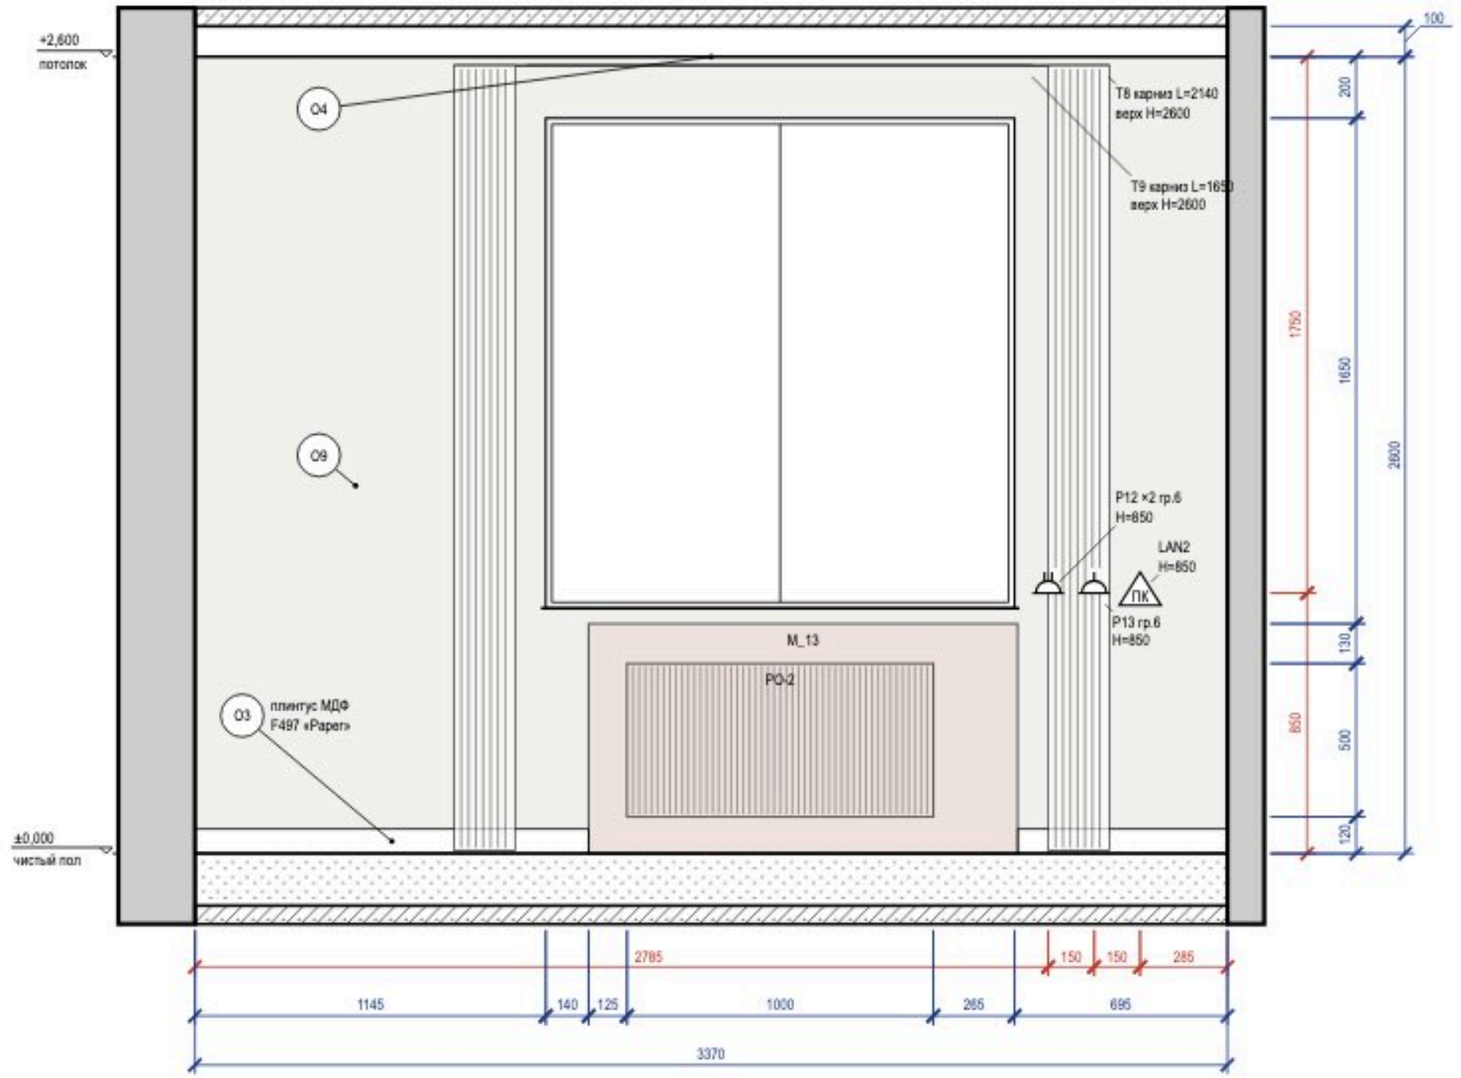


Схема развёрток (М 1:100)

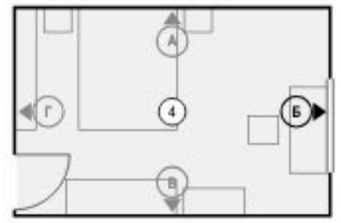

Ведомость отделки (на листе)

Марка	Поверхность	Материал, изделие	Цвет, код	Кол.
О3	плинтус	плинтус МДФ, h 80 мм, аналог: плинтус МДФ под окраску 80×16 мм, полуглянцевая	Tikkurila F497 «Paper»	2 м
О4	потолок	окраска, Tikkurila Anti-Reflex 2, глубокоматовая, подготовка Q3	Tikkurila F497 «Paper»	17,5 м²
О9	стены	окраска, Tikkurila Joker, шелковисто-матовая, подготовка К3	Tikkurila F497 «Paper»	6,3 м²

Примечания

1. Размеры — в мм от чистовых поверхностей стен; условные обозначения и общие указания — лист 2.
2. Карнизы (шины) — по ведомости текстиля декоратора; длина L и верх H — по развёртке, крепление — до окраски потолка.
3. Линии узора (швы плитки, складки штор, рёбра радиаторов) прерываются у знаков и выносок — просвет между линиями не менее 0,7 мм.

					Проект: Четырёхкомнатная квартира
	Лист	№ док.	Подпись	Дата	Развёртка стены Б. Детская 1 (пом. 4)
Дизайнер	Кырпан А.С.			05.10.26	

Стадия	Лист	Листов
П	54	111

выпуск 05.10.2026 № d0efc1af8a · стр. 54 из 111

Развёртка стены В


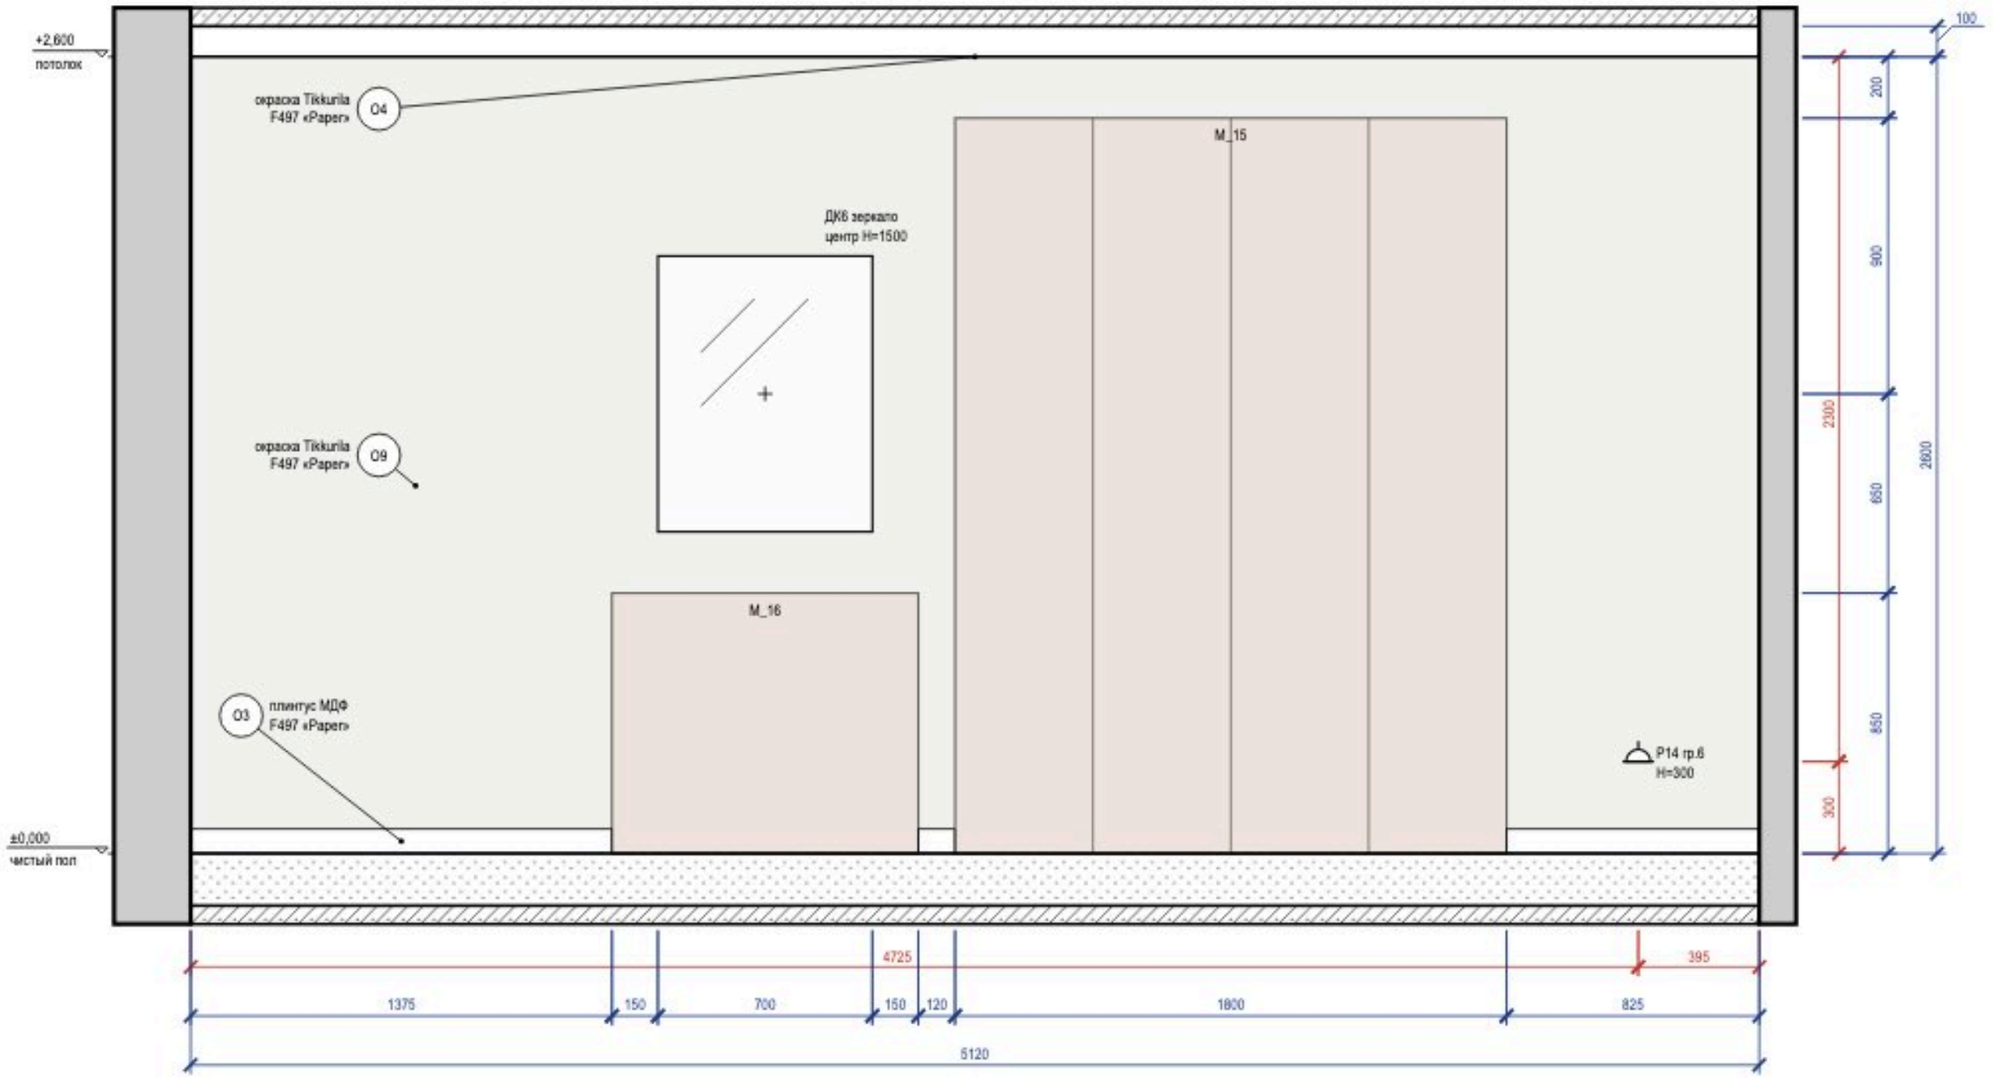



Схема развёрток (М 1:100)

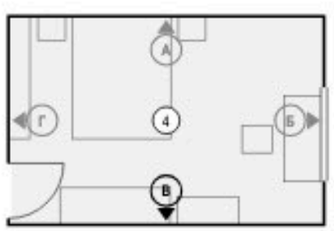

Ведомость отделки (на листе)

Марка	Поверхность	Материал, изделие	Цвет, код	Кол.
О3	плинтус	плинтус МДФ, h 80 мм, аналог: плинтус МДФ под окраску 80×16 мм, полуглянцевая	Tikkurila F497 «Paper»	2,3 м
О4	потолок	окраска, Tikkurila Anti-Reflex 2, глубокоматовая, подготовка О3	Tikkurila F497 «Paper»	17,5 м²
О9	стены	окраска, Tikkurila Joker, шелковисто-матовая, подготовка К3	Tikkurila F497 «Paper»	13,3 м²

Визуализация этой стены — лист 51

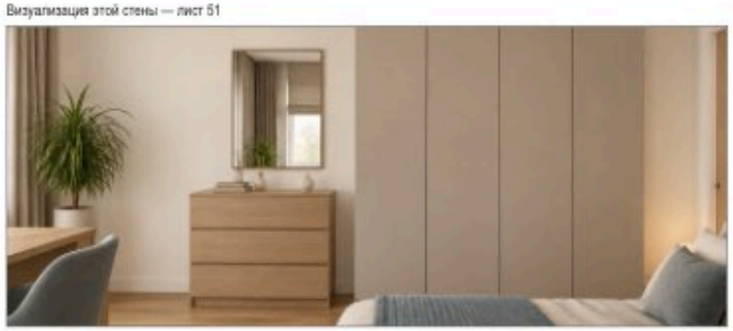

Примечания

1. Размеры — в мм от чистовых поверхностей стен; условные обозначения и общие указания — лист 2.
2. Картины и зеркала крепить к основанию по паспорту изделия (закладные и анкеры — в перечне скрытых работ); крест — ось центра предмета.

					Проект: Четырёхкомнатная квартира
	Лист	№ док.	Подпись	Дата	
Дизайнер	Кырпан А.С.			05.10.26	Развёртка стены В. Детская 1 (пом. 4)

Стадия	Лист	Листов
П	55	111

выпуск 05.10.2026 · d0efc1af8a · стр. 55 из 111

Развёртка стены Г

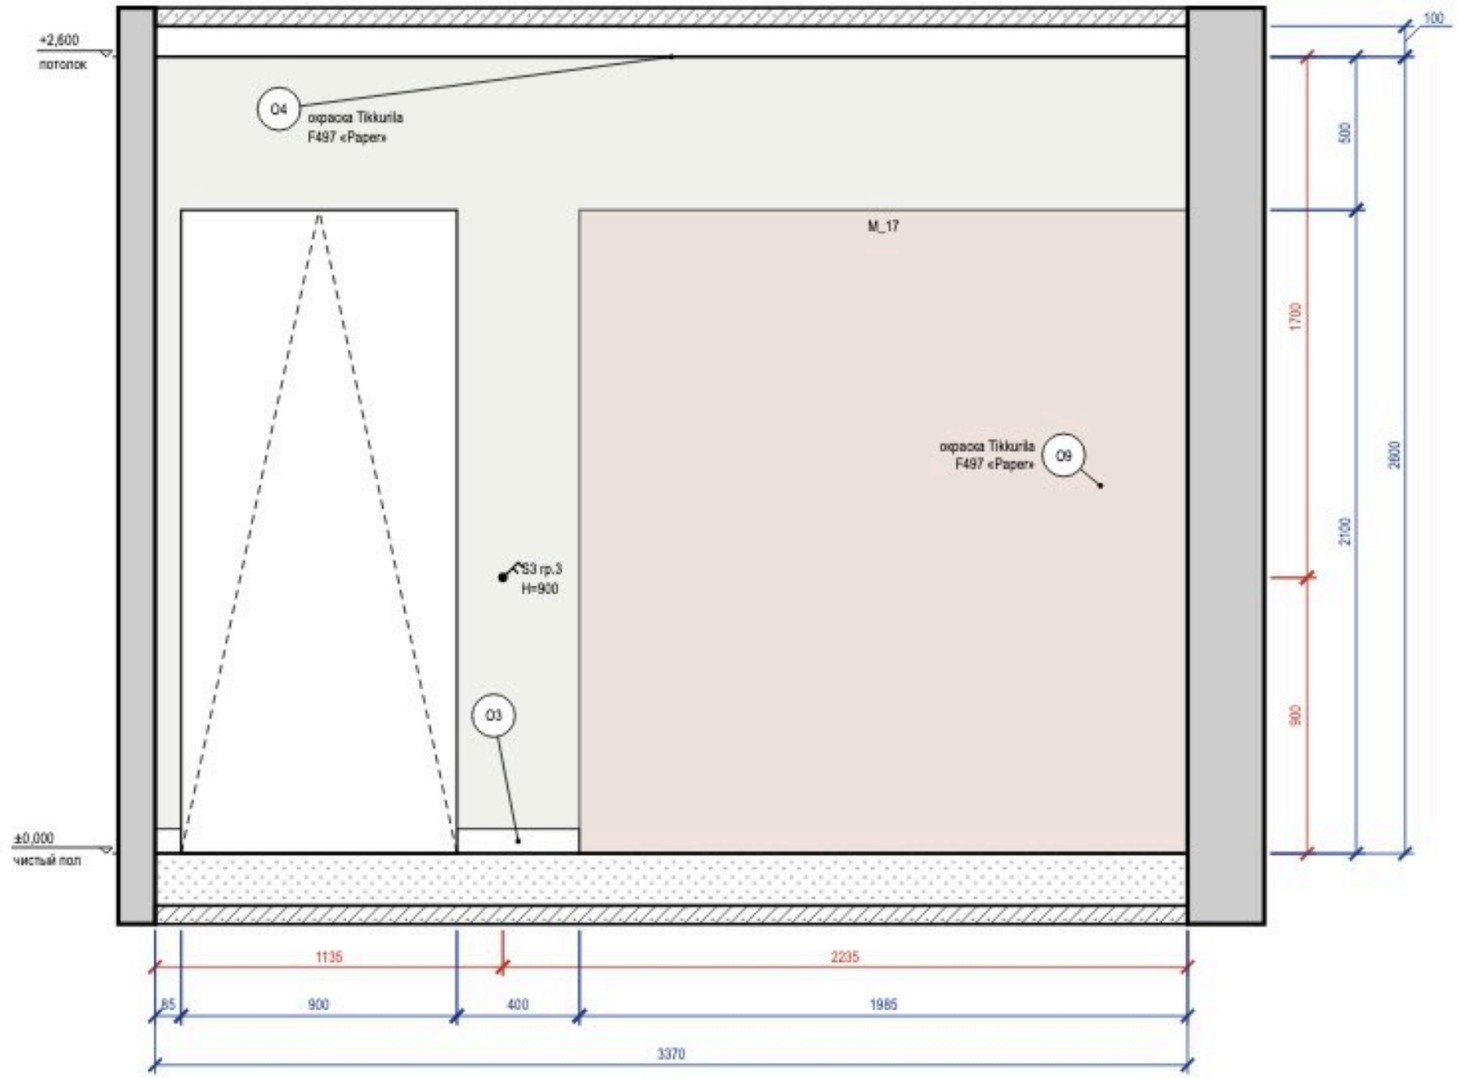



Схема развёрток (М 1:100)



Ведомость отделки (на листе)

Марка	Поверхность	Материал, изделие	Цвет, код	Кол.
О3	плинтус	плинтус МДФ, h 80 мм, аналог: плинтус МДФ под окраску 80×16 мм, полуглянцевая	Tikkurila F497 «Paper»	0,5 м
О4	потолок	окраска, Tikkurila Anti-Reflex 2, глубокоматовая, подготовка Q3	Tikkurila F497 «Paper»	17,5 м²
О9	стены	окраска, Tikkurila Joker, шелковисто-матовая, подготовка К3	Tikkurila F497 «Paper»	6,9 м²

Визуализация этой стены — лист 52

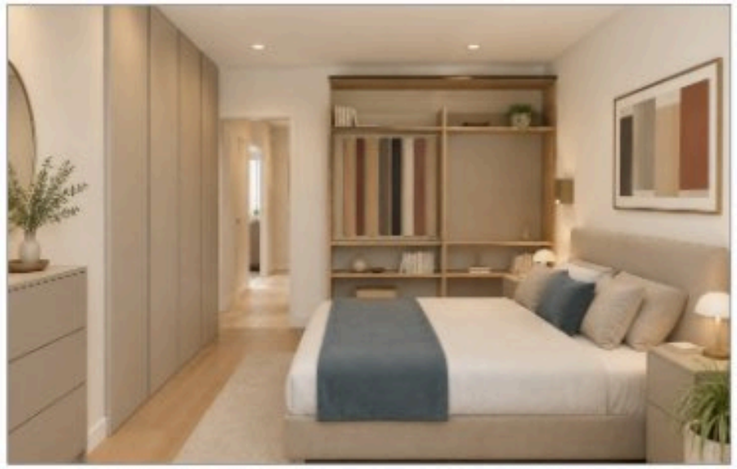

Примечания

1. Размеры — в мм от чистовых поверхностей стен; условные обозначения и общие указания — лист 2.

	Лист	№ док.	Подпись	Дата	Проект: Четырёхкомнатная квартира
Дизайнер	Кырпан А.С.			05.10.26	Развёртка стены Г. Детская 1 (пом. 4)

Стадия	Лист	Листов
П	56	111


выпуск 05.10.2026 · d0efc1af8a · стр. 56 из 111



					Проект: Четырёхкомнатная квартира
	Лист	№ док.	Подпись	Дата	Визуализация коридора
Дизайнер	Кырпан А.С.			05.10.26	

Стадия	Лист	Листов
П	57	111


выпуск 05.10.2026 d0efc1af8a · стр. 57 из 111

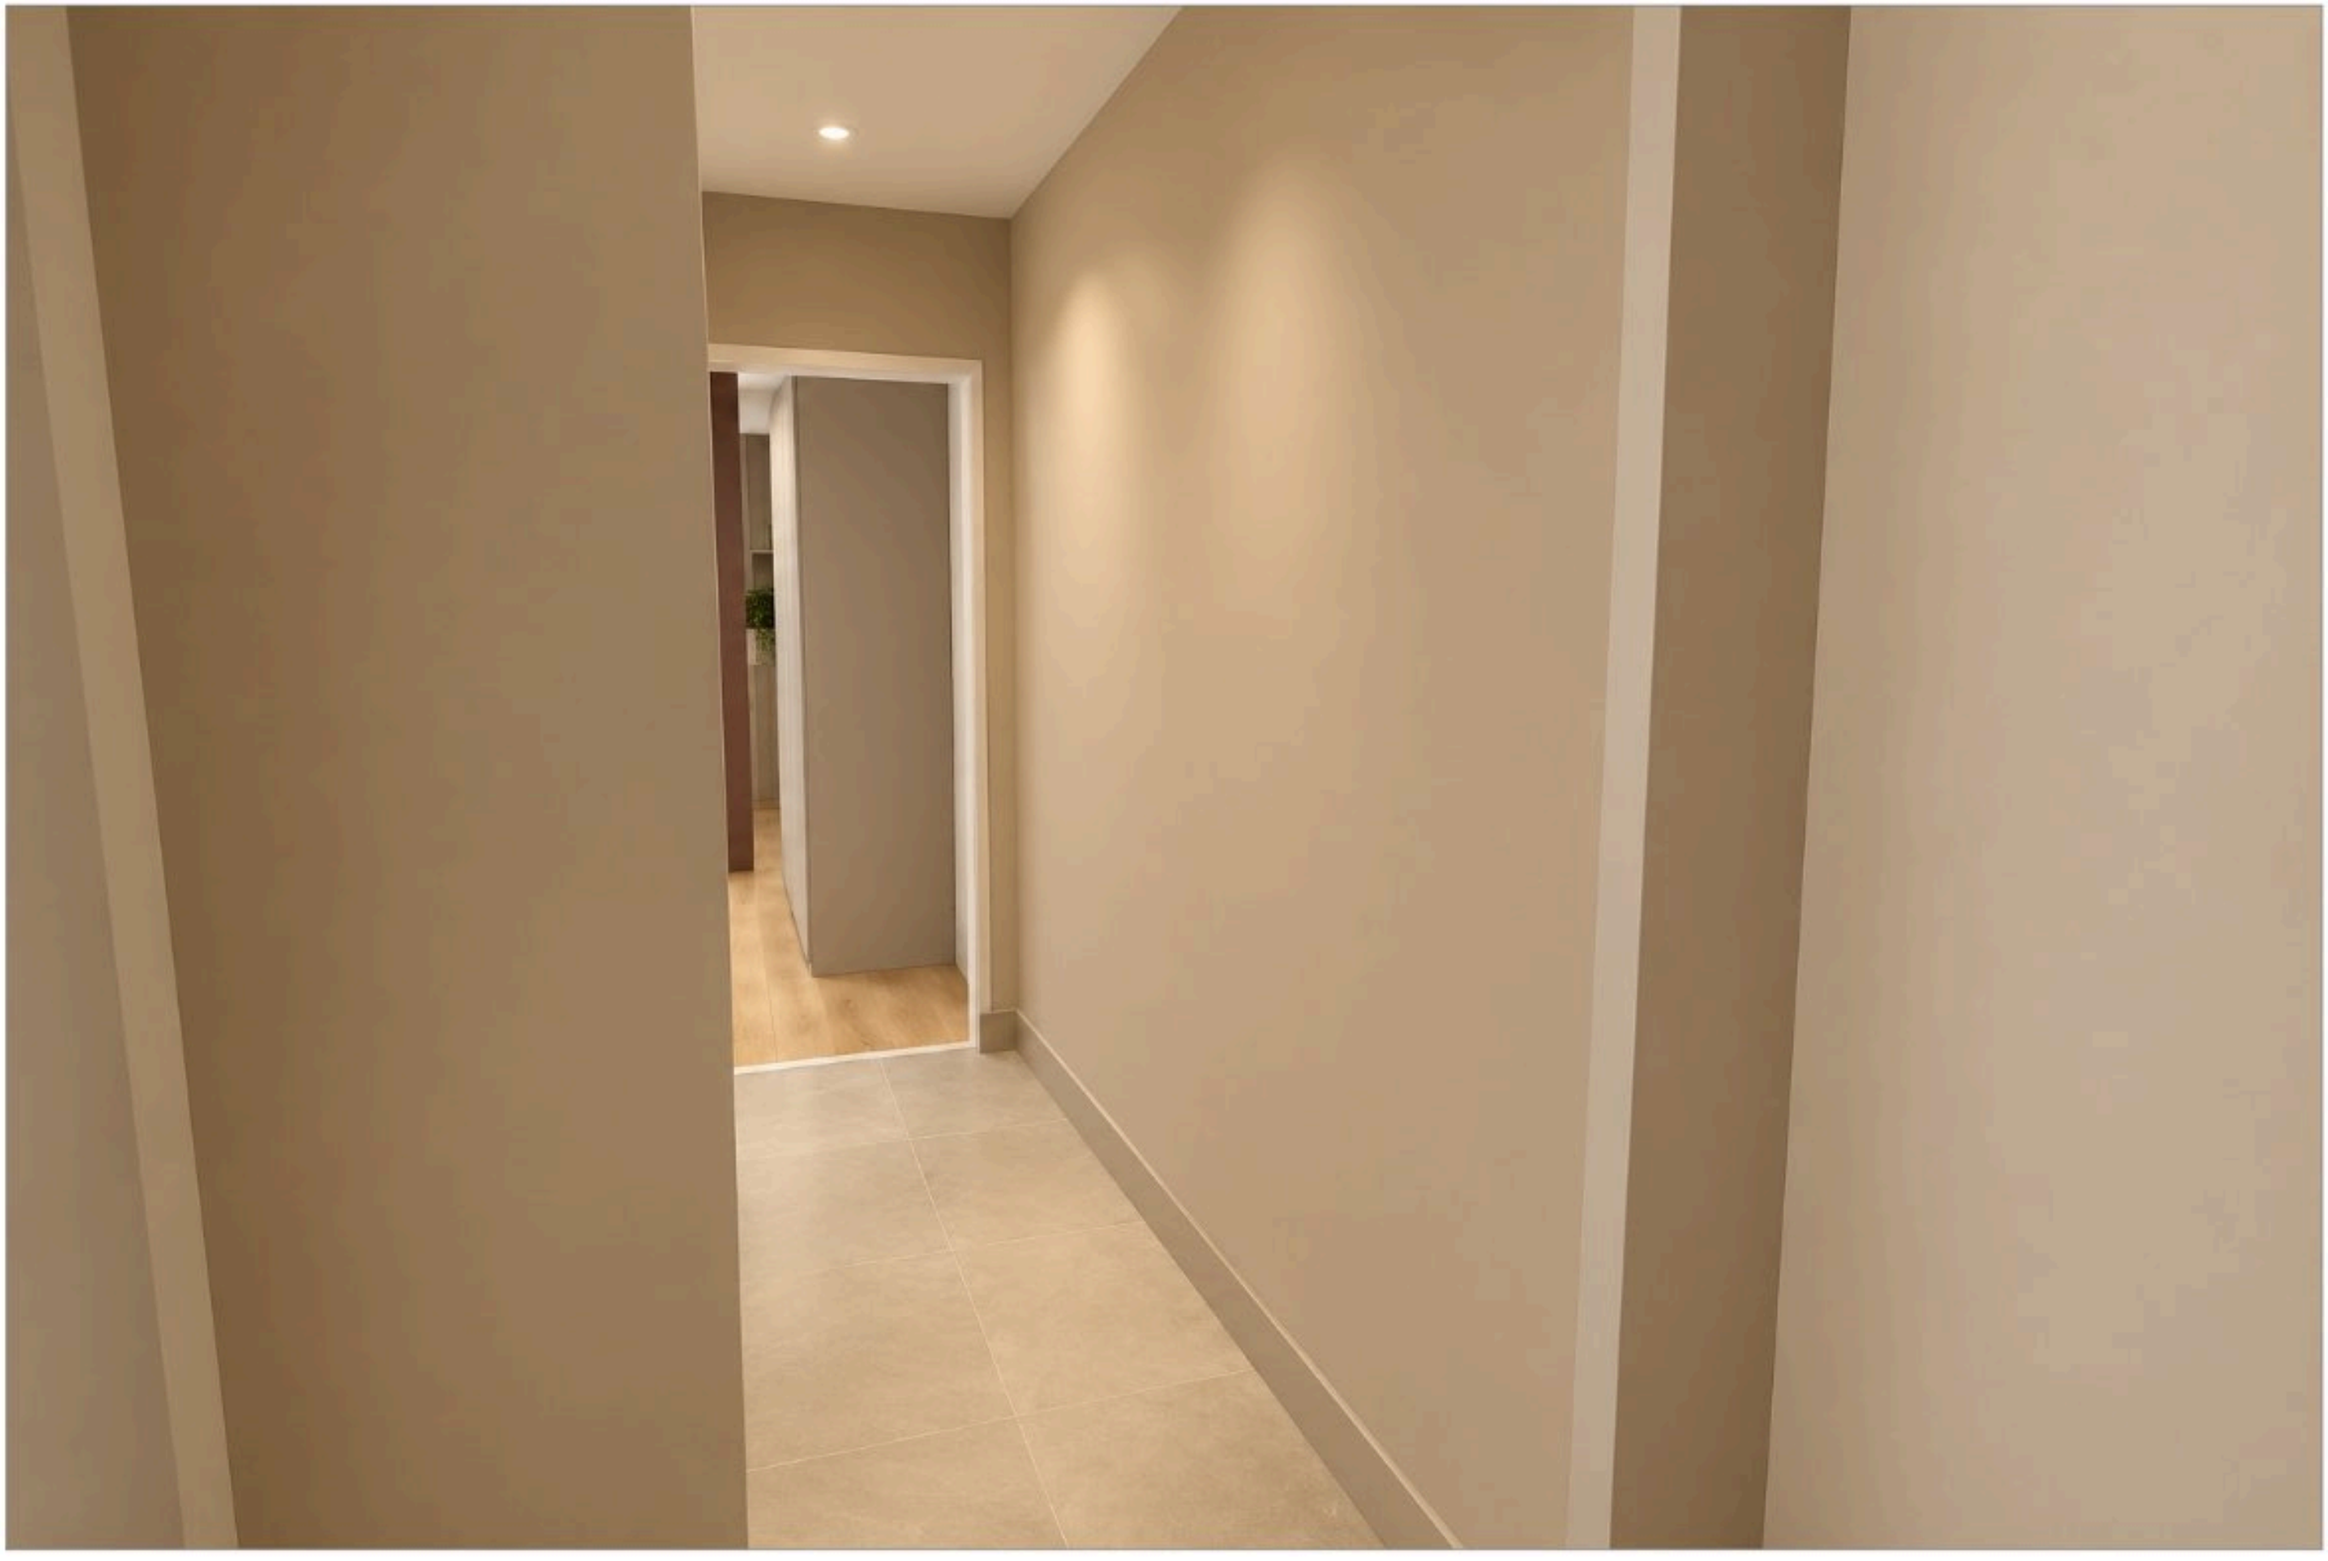

					Проект: Четырёхкомнатная квартира			
	Лист	№ док.	Подпись	Дата	Визуализация коридора	Стадия	Лист	Листов
Дизайнер	Кырпан А.С.			05.10.26		П	58	111

выпуск 05.10.2026 № d0efc1af8a · стр. 58 из 111

Развёртка стены А

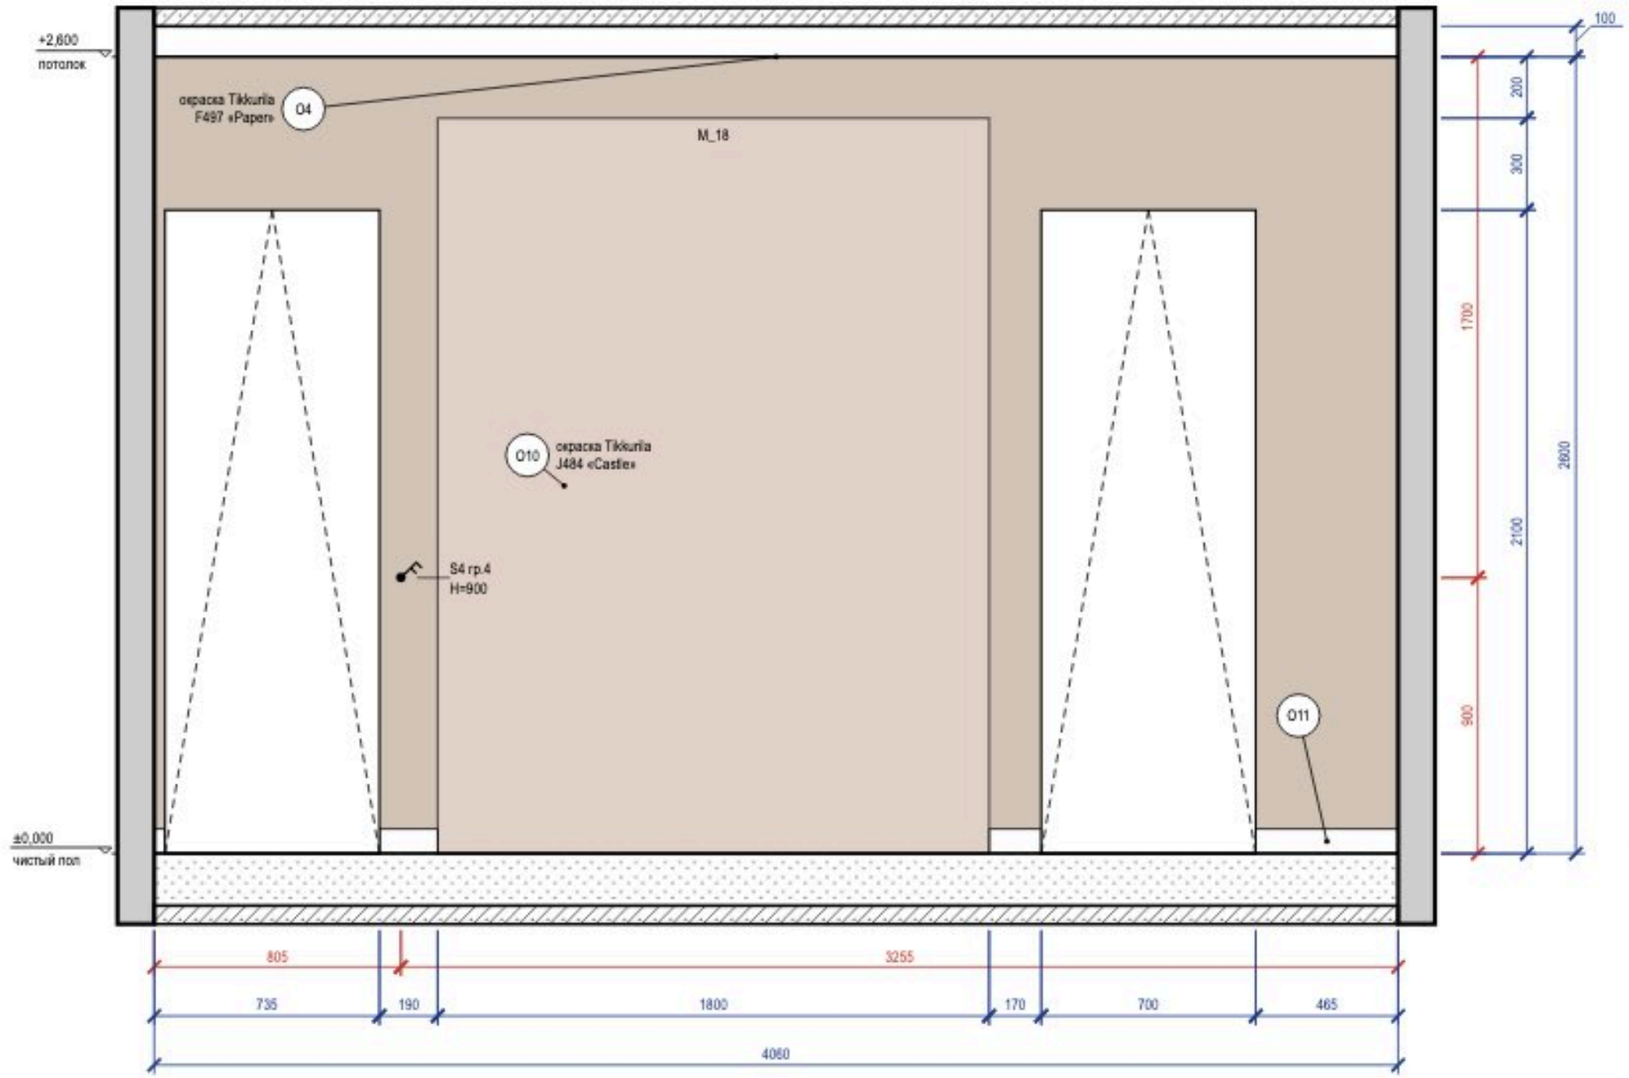

Развёртка стены Б

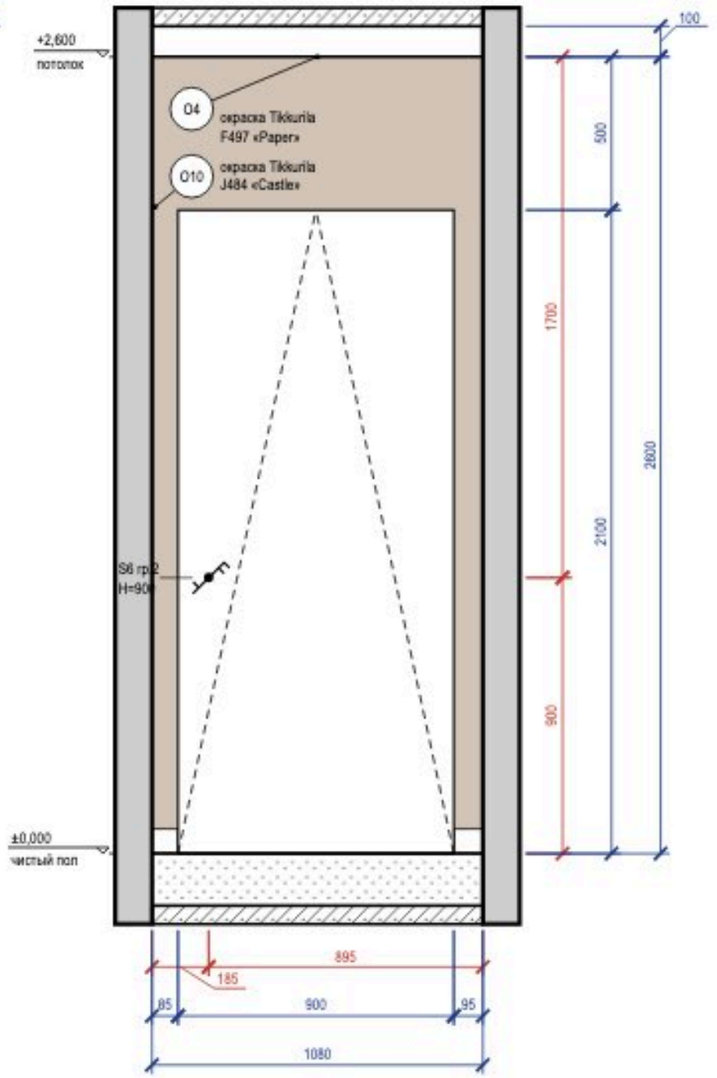


Схема развёрток (М 1:100)



Ведомость отделки (на листе)

Марка	Поверхность	Материал, изделие	Цвет, код	Кол.
O4	потолок	окраска, Tikkurila Anti-Reflex 2, глубокоматовая, подготовка Q3	Tikkurila F497 «Paper»	4,5 м²
O10	стены	окраска, Tikkurila Optiva 20 Semimatt, шелковисто-матовая, подготовка K3	Tikkurila J484 «Castle»	8,5 м²
O11	плинтус	плинтус МДФ, h 80 мм, аналог: плинтус МДФ под окраску 80×16 мм, полуглянцевая	Tikkurila J484 «Castle»	1 м

Визуализация этой стены — лист 57



Примечания

1. Размеры — в мм от чистовых поверхностей стен; условные обозначения и общие указания — лист 2.

					Проект: Четырёхкомнатная квартира
	Лист	№ док.	Подпись	Дата	
Дизайнер	Кырпан А.С.			05.10.26	Развёртки стен А, Б. Коридор (пом. 5)
					Стадия: П; Лист: 59; Листов: 111

выпуск 05.10.2026 · d0efc1af8a · стр. 59 из 111

Развёртка стены В

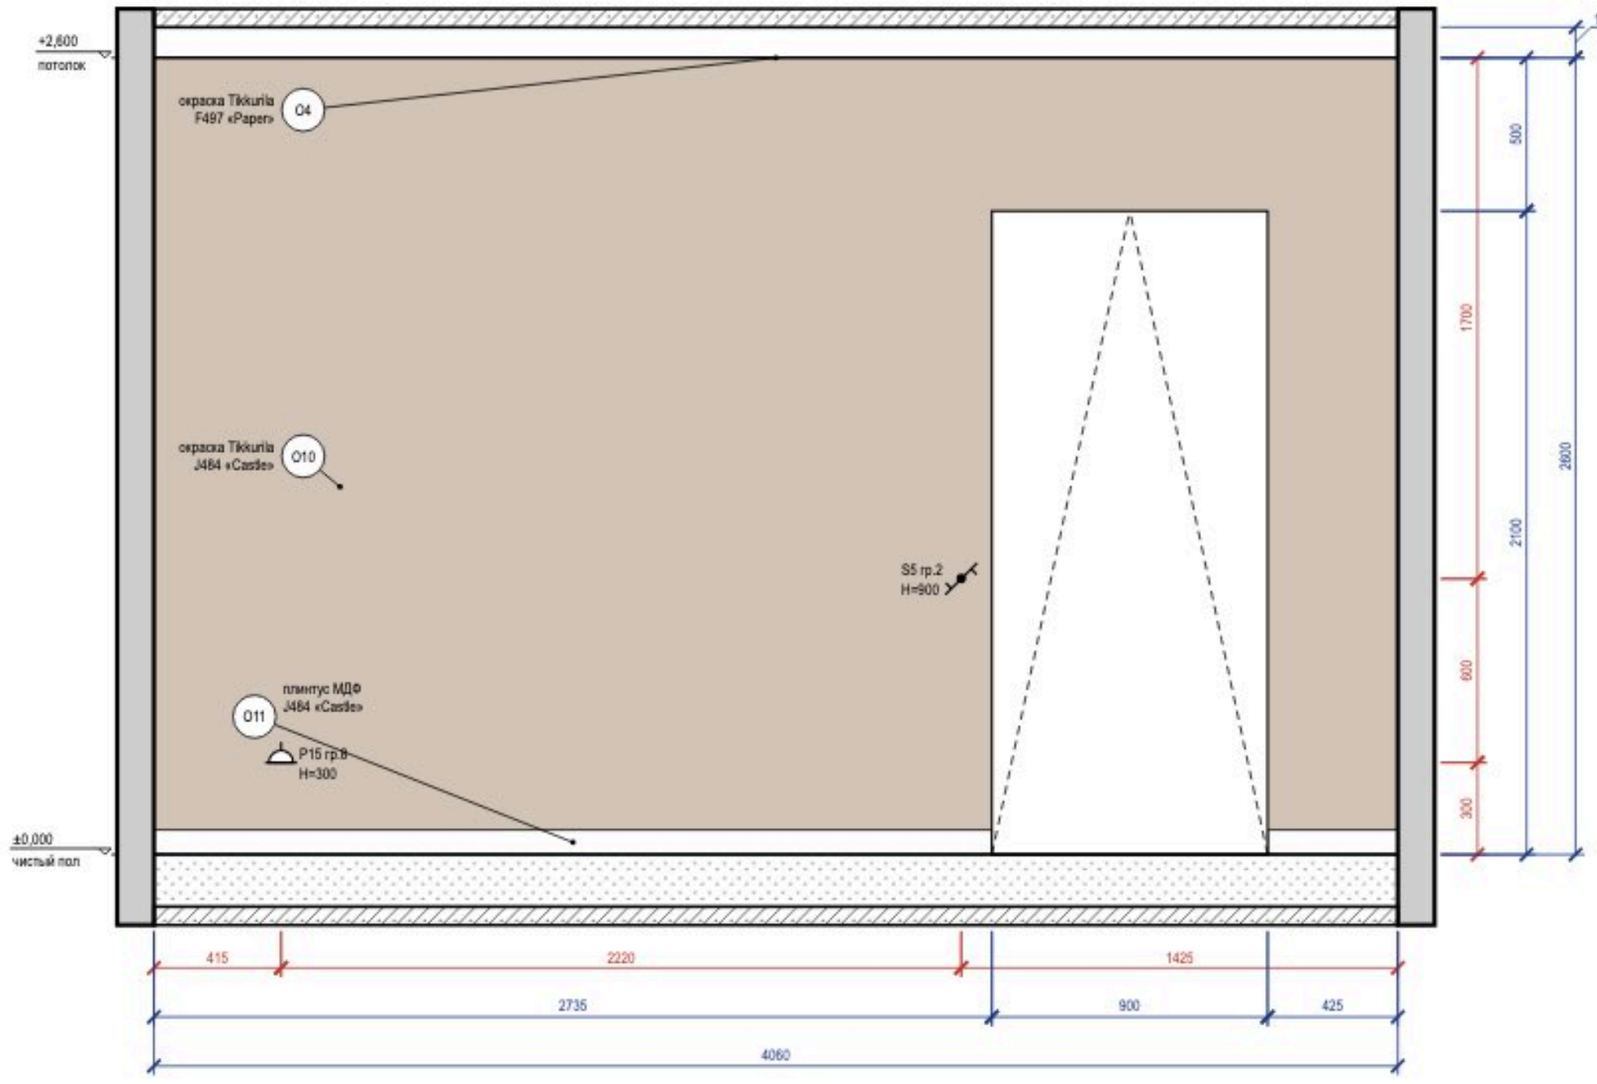



Схема развёрток (М 1:100)



Ведомость отделки (на листе)

Марка	Поверхность	Материал, изделие	Цвет, код	Кол.
О4	потолок	окраска, Tikkurila Anti-Reflex 2, глубокоматовая, подготовка Q3	Tikkurila F497 «Paperi»	4,5 м²
О10	стены	окраска, Tikkurila Optiva 20 Semimatt, шелковисто-матовая, подготовка К3	Tikkurila J484 «Castle»	8,7 м²
О11	плинтус	плинтус МДФ, h 80 мм, аналог: плинтус МДФ под окраску 80×16 мм, полутянцевая	Tikkurila J484 «Castle»	3,2 м

Визуализация этой стены — лист 58

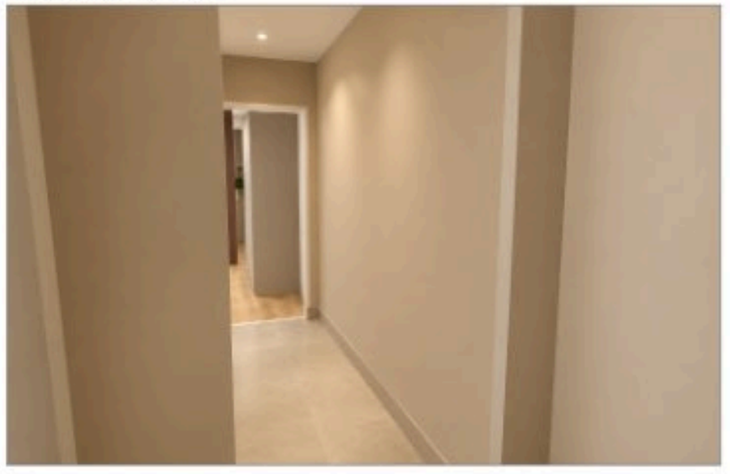

Примечания

1. Размеры — в мм от чистовых поверхностей стен; условные обозначения и общие указания — лист 2.

					Проект: Четырёхкомнатная квартира
	Лист	№ док.	Подпись	Дата	Развёртка стены В. Коридор (пом. 5)
Дизайнер	Кырпан А.С.			05.10.26	

Стадия	Лист	Листов
П	60	111

выпуск 05.10.2026 · d0efc1af8a · стр. 60 из 111



					Проект: Четырёхкомнатная квартира	
	Лист	№ док.	Подпись	Дата		
Дизайнер	Кырпан А.С.			05.10.26	Визуализация кухни	Стадия / Лист / Листов
						П / 61 / 111

выпуск 05.10.2026 · d0efc1af8a · стр. 61 из 111

Развёртка стены А

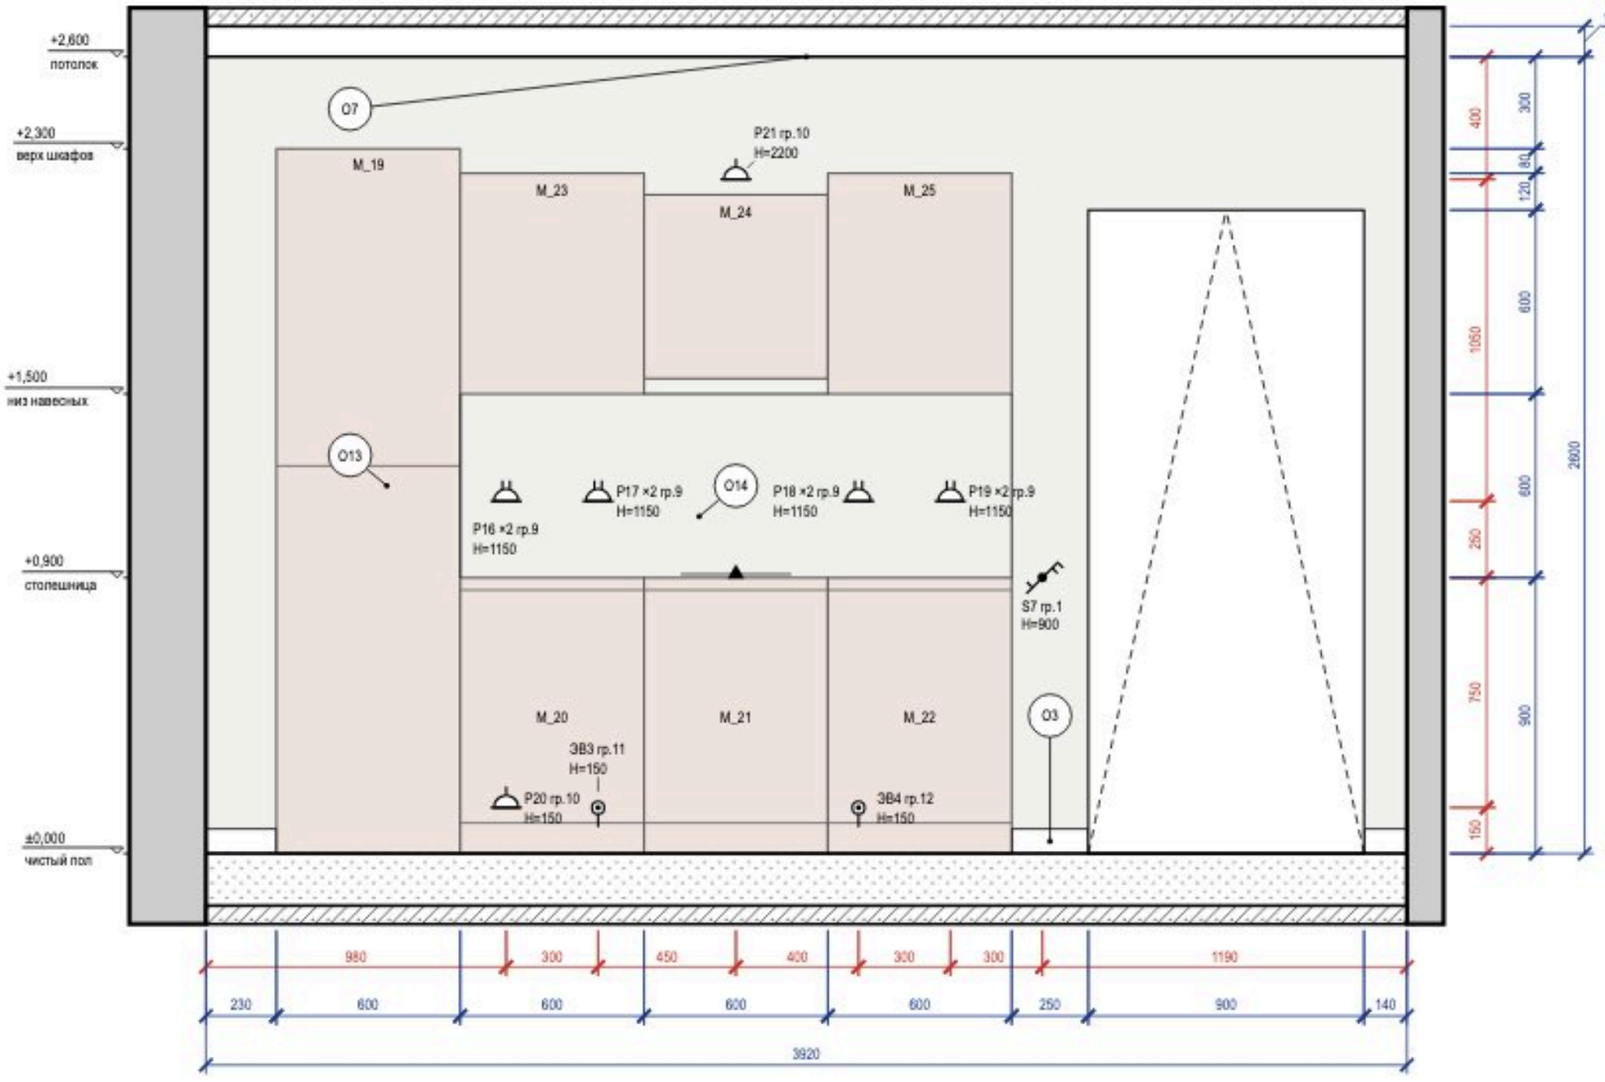


Схема развёрток (М 1:100)



Ведомость отделки (на листе)

Марка	Поверхность	Материал, изделие	Цвет, код	Кол.
О3	плинтус	плинтус МДФ, h 80 мм, аналог: плинтус МДФ под окраску 80×16 мм, полуглянцевая	Tikkurila F497 «Paper»	0,6 м
О7	потолок	окраска, Tikkurila Luja 7, матовая, подготовка Q3	Tikkurila F497 «Paper»	15,2 м²
О13	стены	окраска, Tikkurila Luja 7, шелковисто-матовая, подготовка K3	Tikkurila F497 «Paper»	7,2 м²
О14	фартук	керамогранит, 600×600×9 мм, аналог: керамогранит матовый, тон F497, затирка CG2WA	#F1F1EC «тон Paper F497»	1,1 м²

Визуализация этой стены — лист 61



Примечания

1. Размеры — в мм от чистовых поверхностей стен; условные обозначения и общие указания — лист 2.

	Лист	№ док.	Подпись	Дата	Проект: Четырёхкомнатная квартира
Дизайнер	Кырпан А.С.			05.10.26	Развёртка стены А. Кухня (пом. 6), кухонный фронт

Стадия	Лист	Листов
П	62	111

выпуск 05.10.2026 · d0efc1af8a · стр. 62 из 111

Развёртка стены Б

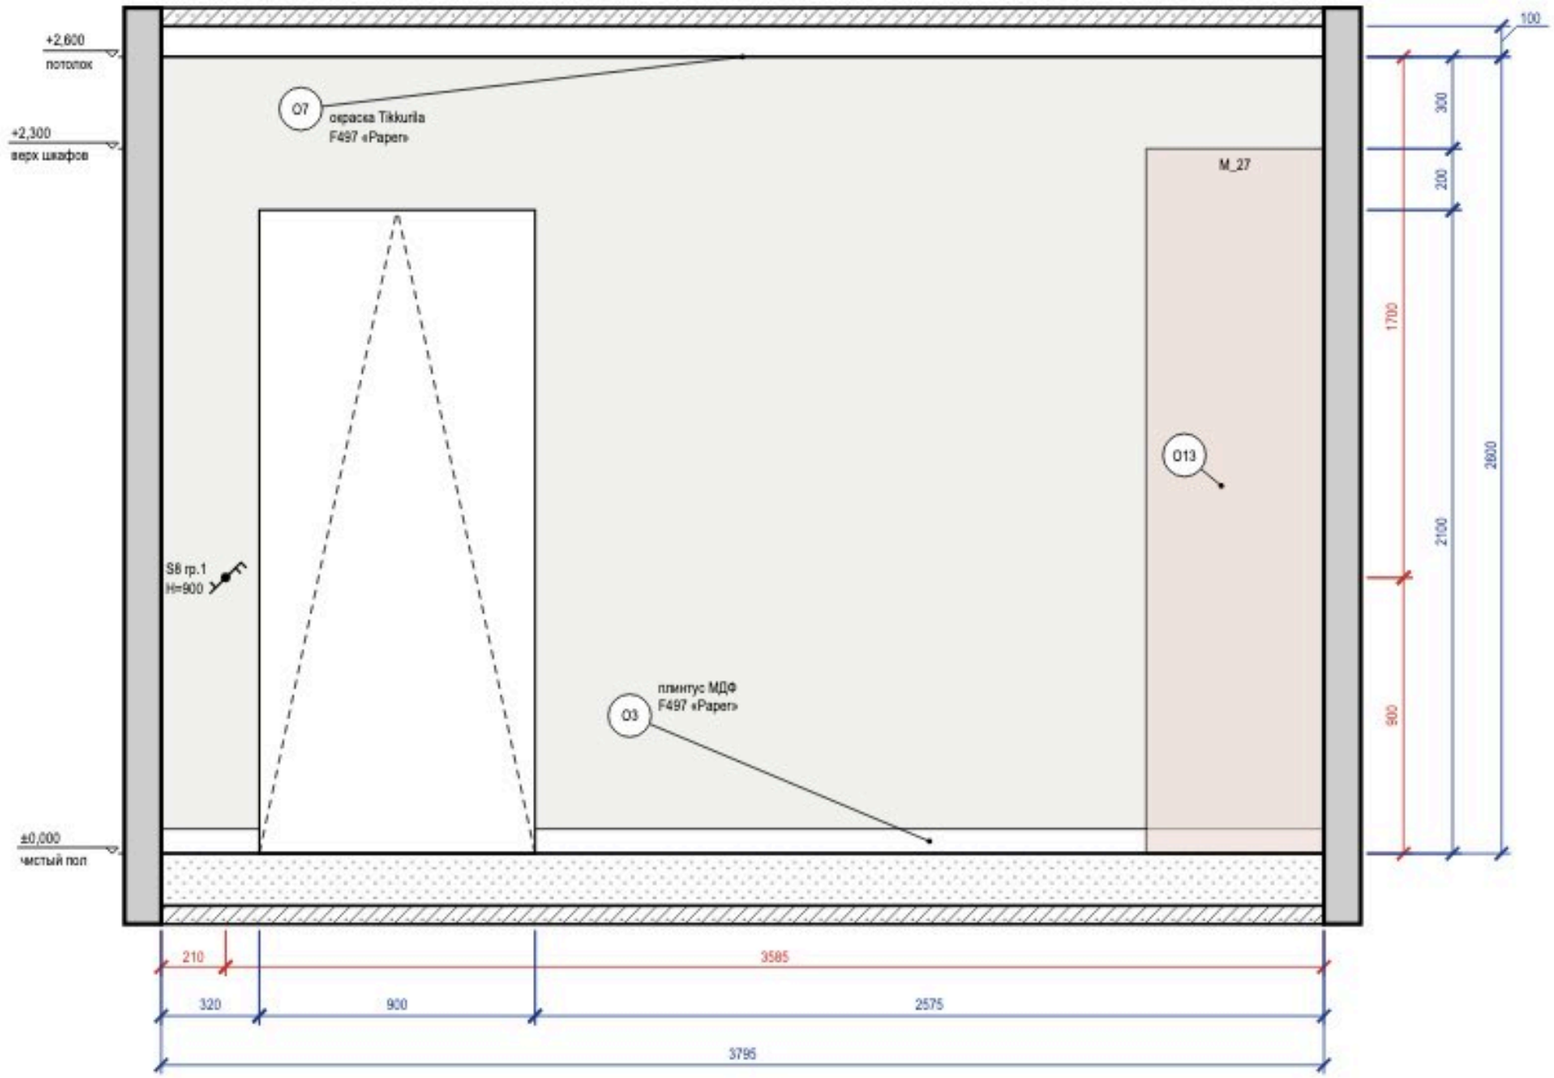


Схема развёрток (М 1:100)



Ведомость отделки (на листе)

Марка	Поверхность	Материал, изделие	Цвет, код	Кол.
О3	плинтус	плинтус МДФ, h 80 мм, аналог: плинтус МДФ под окраску 80×16 мм, полуглянцевая	Tikkurila F497 «Paper»	2,9 м
О7	потолок	окраска, Tikkurila Luja 7, матовая, подготовка Q3	Tikkurila F497 «Paper»	15,2 м²
О13	стены	окраска, Tikkurila Luja 7, шелковисто-матовая, подготовка К3	Tikkurila F497 «Paper»	8 м²

Примечания

1. Размеры — в мм от чистовых поверхностей стен; условные обозначения и общие указания — лист 2.

					Проект: Четырёхкомнатная квартира
	Лист	№ док.	Подпись	Дата	Развёртка стены Б. Кухня (пом. 6)
Дизайнер	Кырпан А.С.			05.10.26	

Стадия	Лист	Листов
П	63	111

выпуск 05.10.2026 № d0efc1af8a · стр. 63 из 111

Развёртка стены В

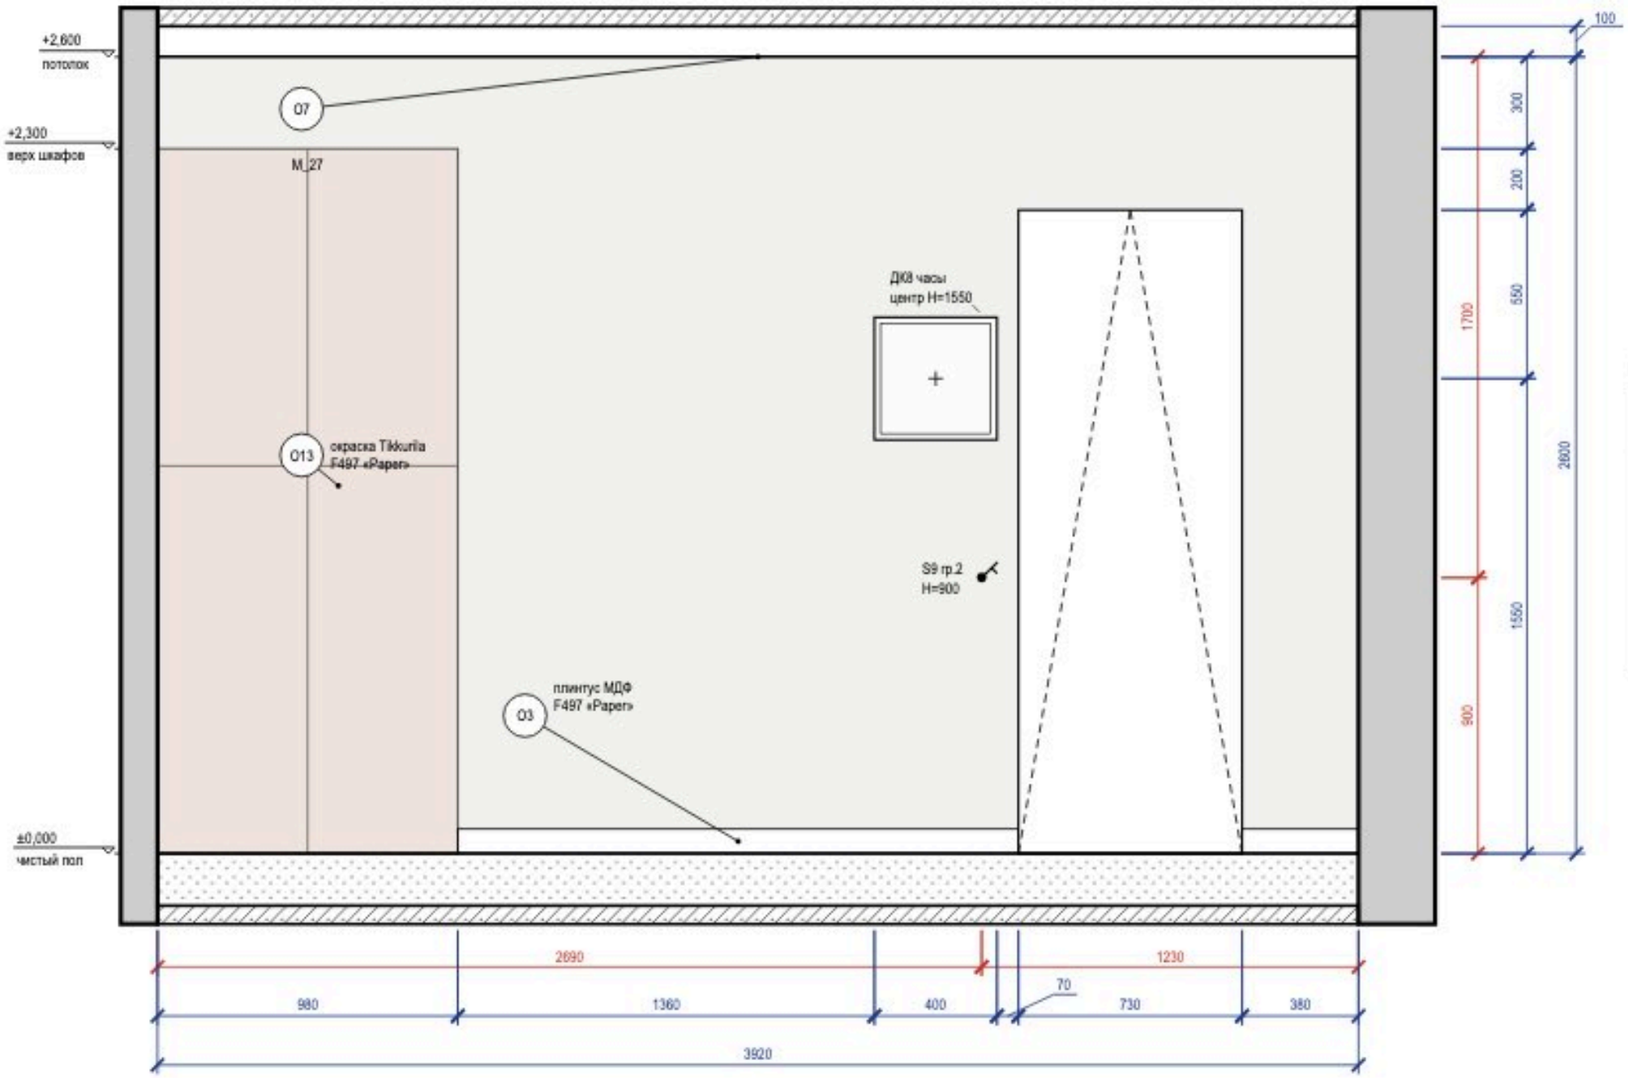


Схема развёрток (М 1:100)



Ведомость отделки (на листе)

Марка	Поверхность	Материал, изделие	Цвет, код	Кол.
О3	плинтус	плинтус МДФ, h 80 мм, аналог: плинтус МДФ под окраску 80×16 мм, полуглянцевая	Tikkurila F497 «Paperi»	2,2 м
О7	потолок	окраска, Tikkurila Luja 7, матовая, подготовка Q3	Tikkurila F497 «Paperi»	15,2 м²
О13	стены	окраска, Tikkurila Luja 7, шелковисто-матовая, подготовка Ю3	Tikkurila F497 «Paperi»	8,7 м²

Примечания

1. Размеры — в мм от чистовых поверхностей стен; условные обозначения и общие указания — лист 2.
2. Картины и зеркала крепить к основанию по паспорту изделия (закладные и анкеры — в перечне скрытых работ); крест — ось центра предмета.

					Проект: Четырёхкомнатная квартира
	Лист	№ док.	Подпись	Дата	
Дизайнер	Кырпан А.С.			05.10.26	Развёртка стены В. Кухня (пом. 6)

Стадия	Лист	Листов
П	64	111

выпуск 05.10.2026 · d0efc1af8a · стр. 64 из 111

Развёртка стены Г

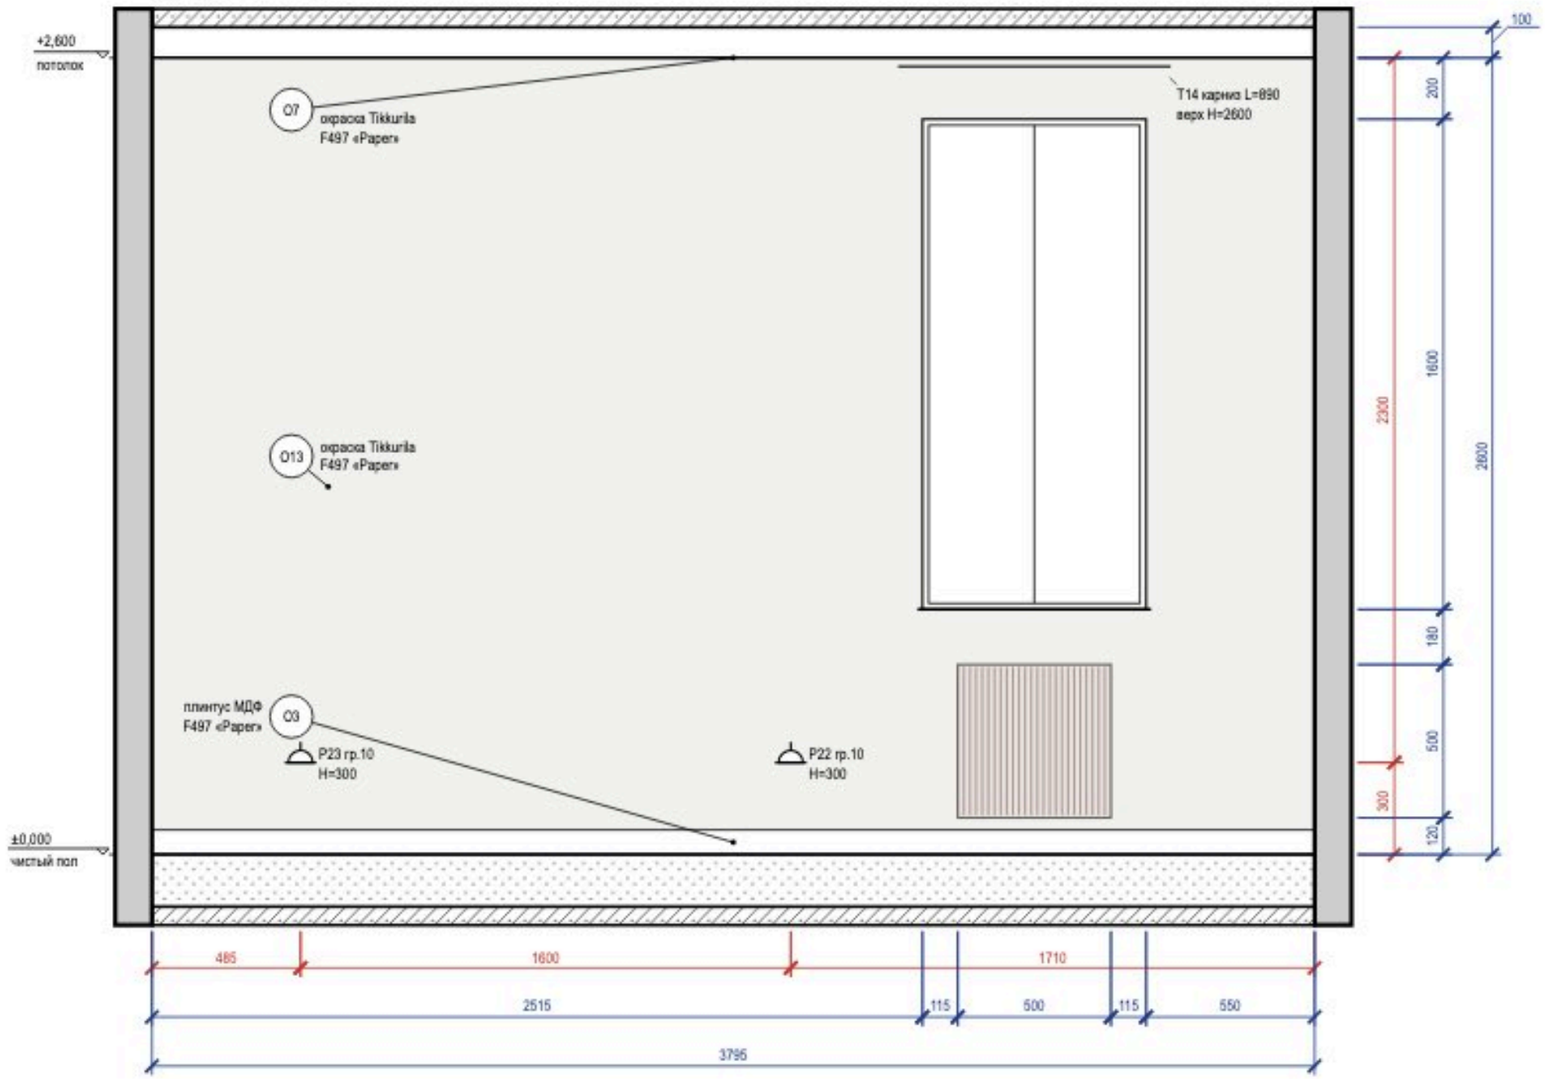


Схема развёрток (М 1:100)



Ведомость отделки (на листе)

Марка	Поверхность	Материал, изделие	Цвет, код	Кол.
О3	плинтус	плинтус МДФ, h 80 мм, аналог: плинтус МДФ под окраску 80×16 мм, полуглянцевая	Tikkurila F497 «Paper»	3,8 м
О7	потолок	окраска, Tikkurila Luja 7, матовая, подготовка Q3	Tikkurila F497 «Paper»	15,2 м²
О13	стены	окраска, Tikkurila Luja 7, шелковисто-матовая, подготовка К3	Tikkurila F497 «Paper»	8,7 м²

Примечания

1. Размеры — в мм от чистовых поверхностей стен; условные обозначения и общие указания — лист 2.
2. Карнизы (шины) — по ведомости текстиля декоратора; длина L и верх H — по развёртке, крепление — до окраски потолка.

					Проект: Четырёхкомнатная квартира
	Лист	№ док.	Подпись	Дата	Развёртка стены Г. Кухня (пом. 6)
Дизайнер	Кырпан А.С.			05.10.26	

Стадия	Лист	Листов
П	65	111

выпуск 05.10.2026 · d0efc1af8a · стр. 65 из 111



					Проект: Четырёхкомнатная квартира
	Лист	№ док.	Подпись	Дата	
Дизайнер	Кырпан А.С.			05.10.26	Визуализация: Прихожая-коридор

Стадия	Лист	Листов
П	66	111

выпуск 05.10.2026 d0efc1af8a · стр. 66 из 111

Развёртка стены А

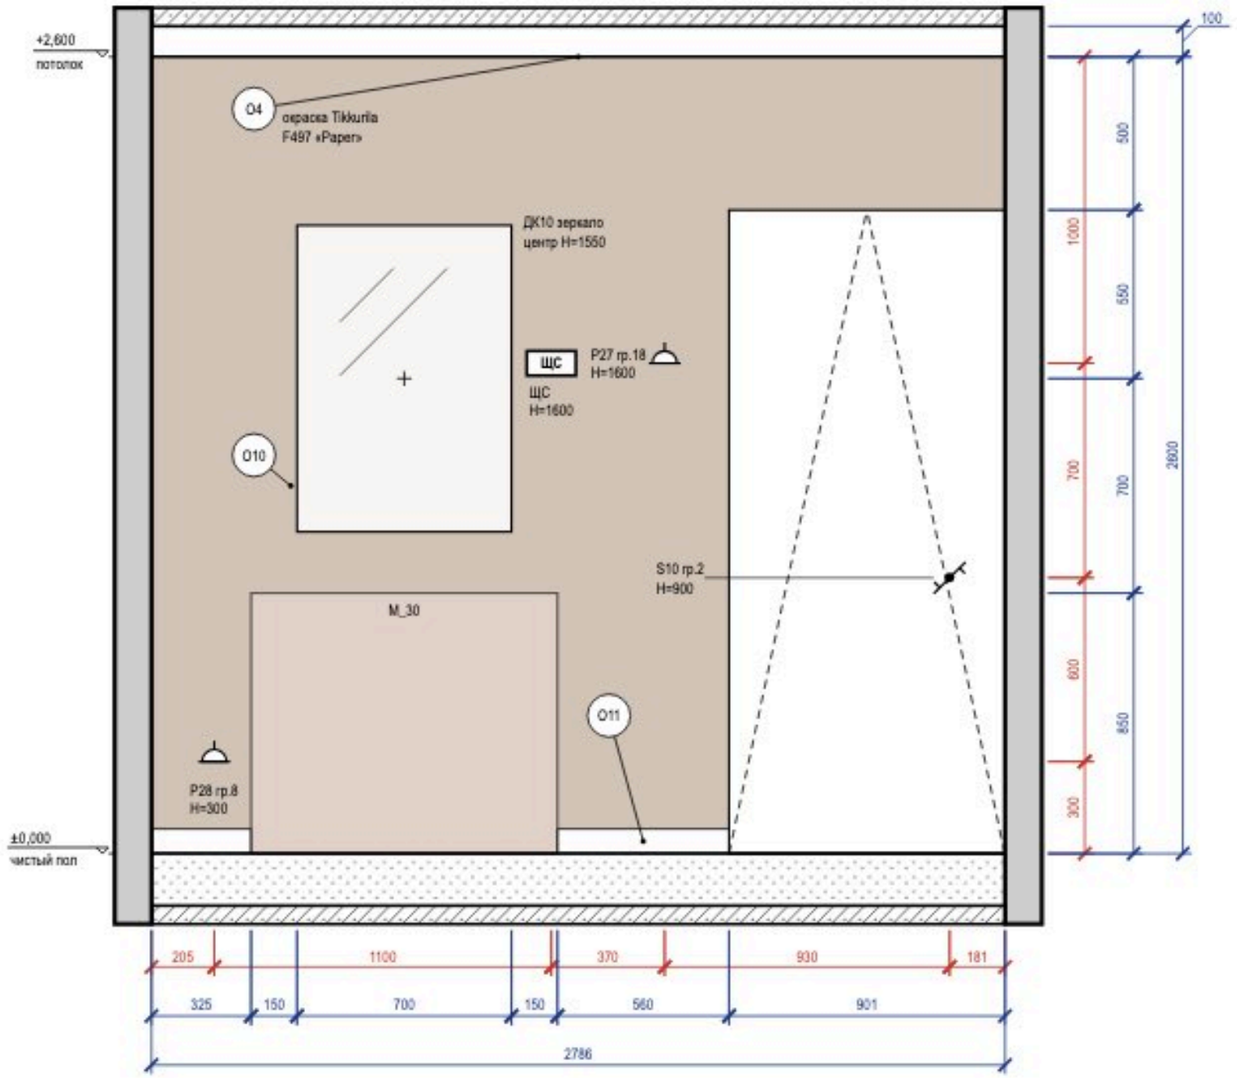



Схема развёрток (М 1:100)



Ведомость отделки (на листе)

Марка	Поверхность	Материал, изделие	Цвет, код	Кол.
О4	потолок	окраска, Tikkurila Anti-Reflex 2, глубокоматовая, подготовка Q3	Tikkurila F497 «Paper»	7,8 м²
О10	стены	окраска, Tikkurila Optiva 20 Semimatt, шелковисто-матовая, подготовка К3	Tikkurila J484 «Castle»	5,4 м²
О11	плинтус	плинтус МДФ, h 80 мм, аналог: плинтус МДФ под окраску 80×16 мм, полуглянцевая	Tikkurila J484 «Castle»	0,9 м

Визуализация этой стены — лист 66

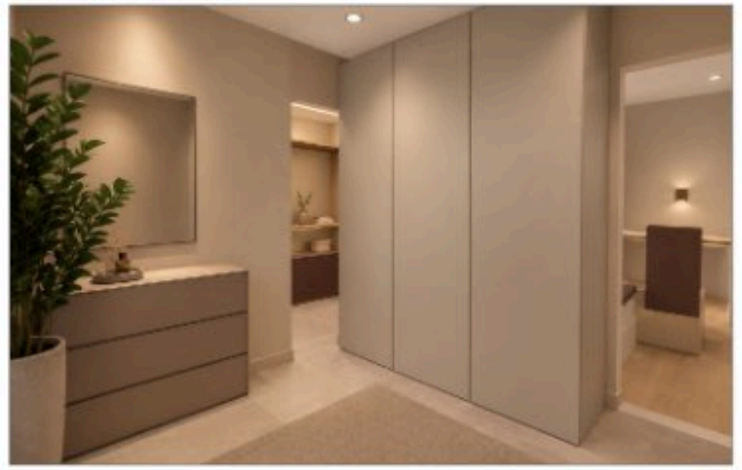

Примечания

1. Размеры — в мм от чистовых поверхностей стен; условные обозначения и общие указания — лист 2.
2. Картины и зеркала крепить к основанию по паспорту изделия (закладные и анкеры — в перечне скрытых работ); крест — ось центра предмета.

					Проект: Четырёхкомнатная квартира
	Лист	№ док.	Подпись	Дата	Развёртка стены А. Прихожая-коридор (пом. 7)
Дизайнер	Кырпан А.С.			05.10.26	

Стадия	Лист	Листов
П	67	111

выпуск 05.10.2026 № d0efc1af8a · стр. 67 из 111

Развёртка стены Б

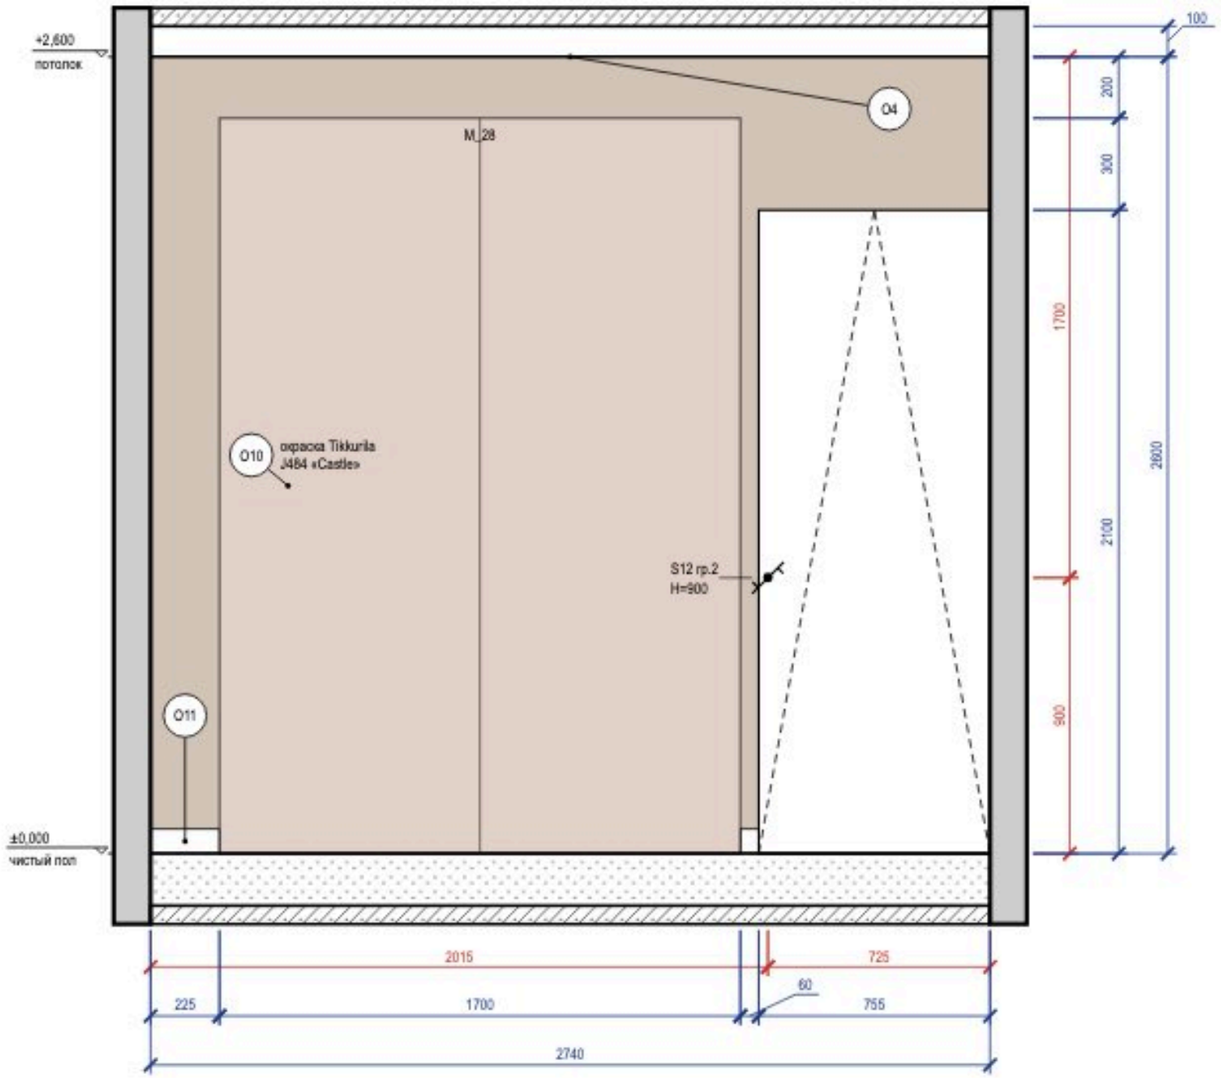


Схема развёрток (М 1:100)



Ведомость отделки (на листе)

Марка	Поверхность	Материал, изделие	Цвет, код	Кол.
О4	потолок	окраска, Tikkurila Anti-Reflex 2, глубокоматовая, подготовка Q3	Tikkurila F497 «Paper»	7,8 м²
О10	стены	окраска, Tikkurila Optiva 20 Semimatt, шелковисто-матовая, подготовка К3	Tikkurila J484 «Castle»	5,5 м²
О11	плинтус	плинтус МДФ, h 80 мм, аналог: плинтус МДФ под окраску 80×16 мм, полуглянцевая	Tikkurila J484 «Castle»	0,3 м

Примечания

1. Размеры — в мм от чистовых поверхностей стен; условные обозначения и общие указания — лист 2.
2. Дверь заходит за угол помещения: на развёртке показана видимая часть проёма 770 из 900 мм — проверить привязку двери в модели.

					Проект: Четырёхкомнатная квартира		
	Лист	№ док.	Подпись	Дата	Развёртка стены Б. Прихожая-коридор (пом. 7)	Стадия	Лист	Листов
Дизайнер	Кырпан А.С.			05.10.26		П	68	111

выпуск 05.10.2026 · d0efc1af8a · стр. 68 из 111

Развёртка стены В

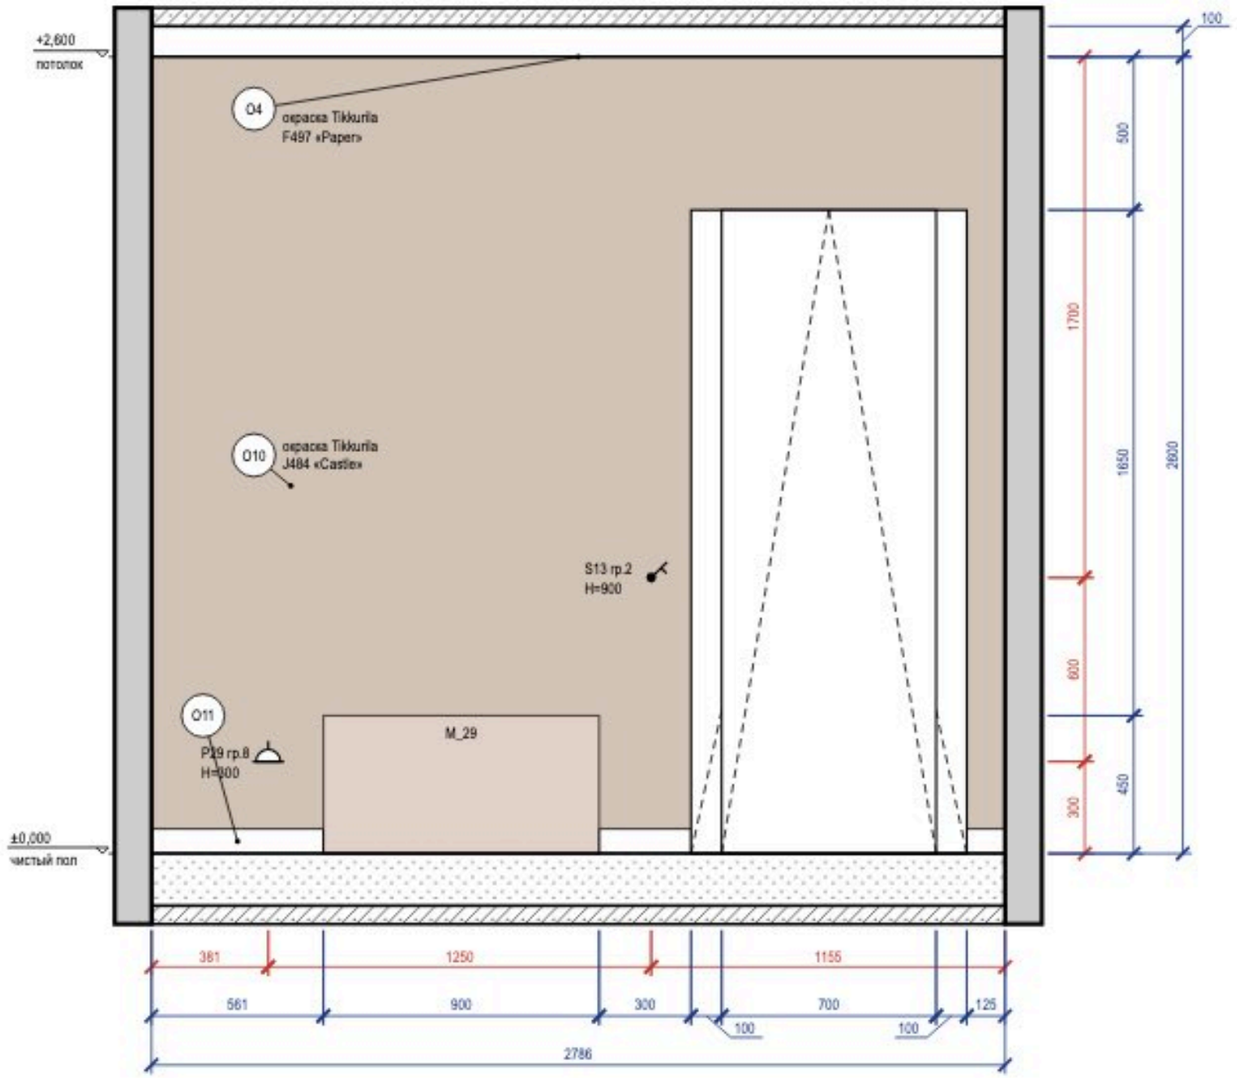


Схема развёрток (М 1:100)



Ведомость отделки (на листе)

Марка	Поверхность	Материал, изделие	Цвет, код	Кол.
О4	потолок	окраска, Tikkurila Anti-Reflex 2, глубокоматовая, подготовка Q3	Tikkurila F497 «Paper»	7,8 м²
О10	стены	окраска, Tikkurila Optiva 20 Semimatt, шелковисто-матовая, подготовка К3	Tikkurila J484 «Castle»	3,9 м²
О11	плинтус	плинтус МДФ, h 80 мм, аналог: плинтус МДФ под окраску 80×16 мм, полуглянцевая	Tikkurila J484 «Castle»	1 м

Примечания

1. Размеры — в мм от чистовых поверхностей стен; условные обозначения и общие указания — лист 2.

					Проект: Четырёхкомнатная квартира
	Лист	№ док.	Подпись	Дата	Развёртка стены В. Прихожая-коридор (пом. 7)
Дизайнер	Кырпан А.С.			05.10.26	

Стадия	Лист	Листов
П	69	111

выпуск 05.10.2026 № d0efc1af8a · стр. 69 из 111

Развёртка стены Г

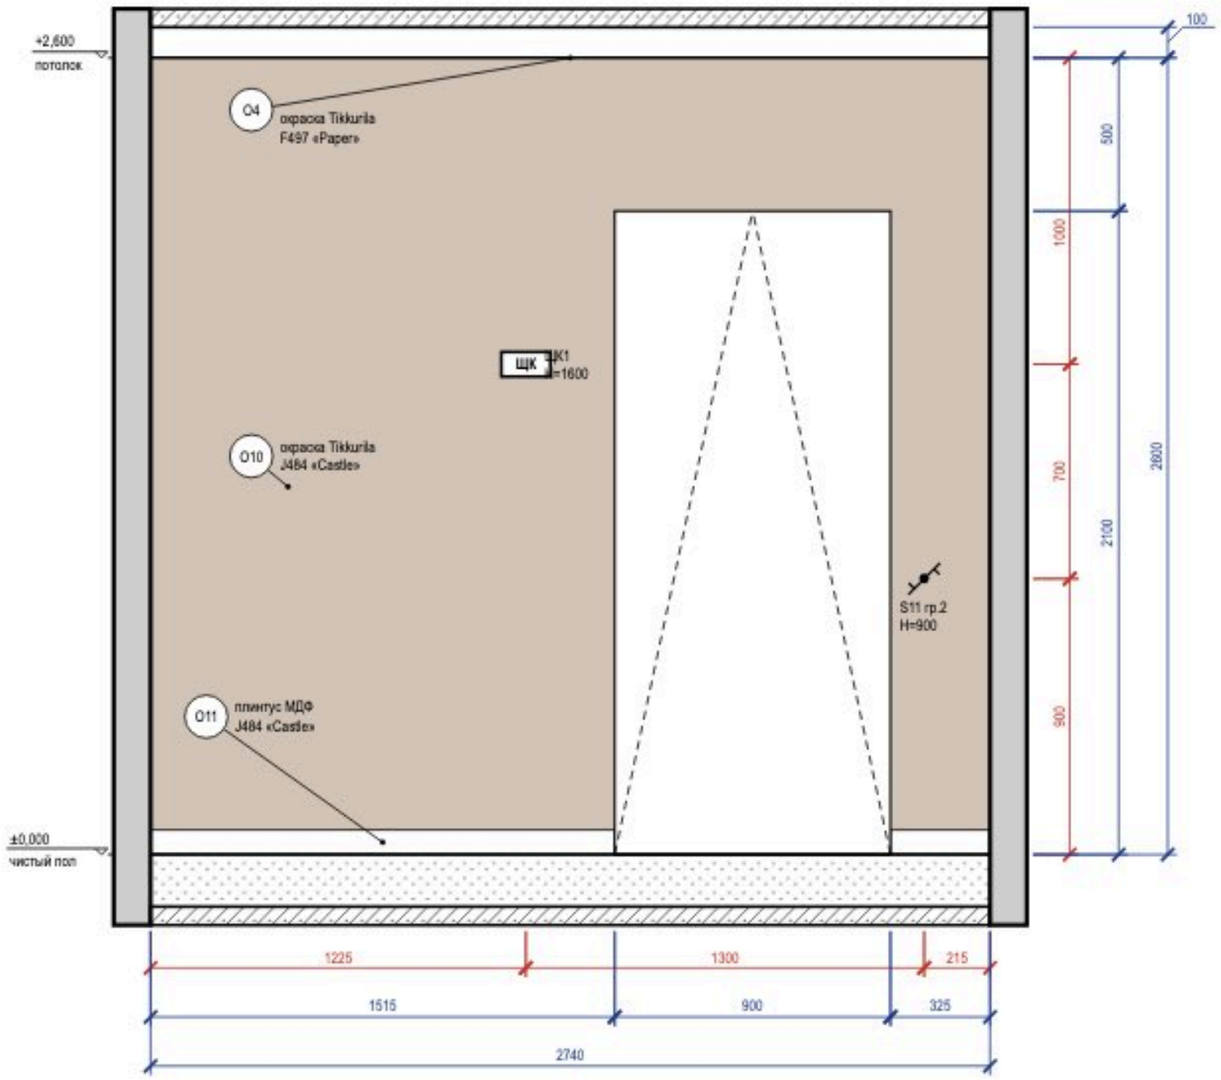


Схема развёрток (М 1:100)



Ведомость отделки (на листе)

Марка	Поверхность	Материал, изделие	Цвет, код	Кол.
О4	потолок	окраска, Tikkurila Anti-Reflex 2, глубокоматовая, подготовка Q3	Tikkurila F497 «Paper»	7,8 м²
О10	стены	окраска, Tikkurila Optiva 20 Semimatt, шелковисто-матовая, подготовка К3	Tikkurila J484 «Castle»	5,2 м²
О11	плинтус	плинтус МДФ, h 80 мм, аналог: плинтус МДФ под окраску 80×16 мм, полуглянцевая	Tikkurila J484 «Castle»	1,8 м


Примечания

1. Размеры — в мм от чистовых поверхностей стен; условные обозначения и общие указания — лист 2.

					Проект: Четырёхкомнатная квартира
	Лист	№ док.	Подпись	Дата	Развёртка стены Г. Прихожая-коридор (пом. 7)
Дизайнер	Кырпан А.С.			05.10.26	

Стадия	Лист	Листов
П	70	111

выпуск 05.10.2026 · d0efc1af8a · стр. 70 из 111

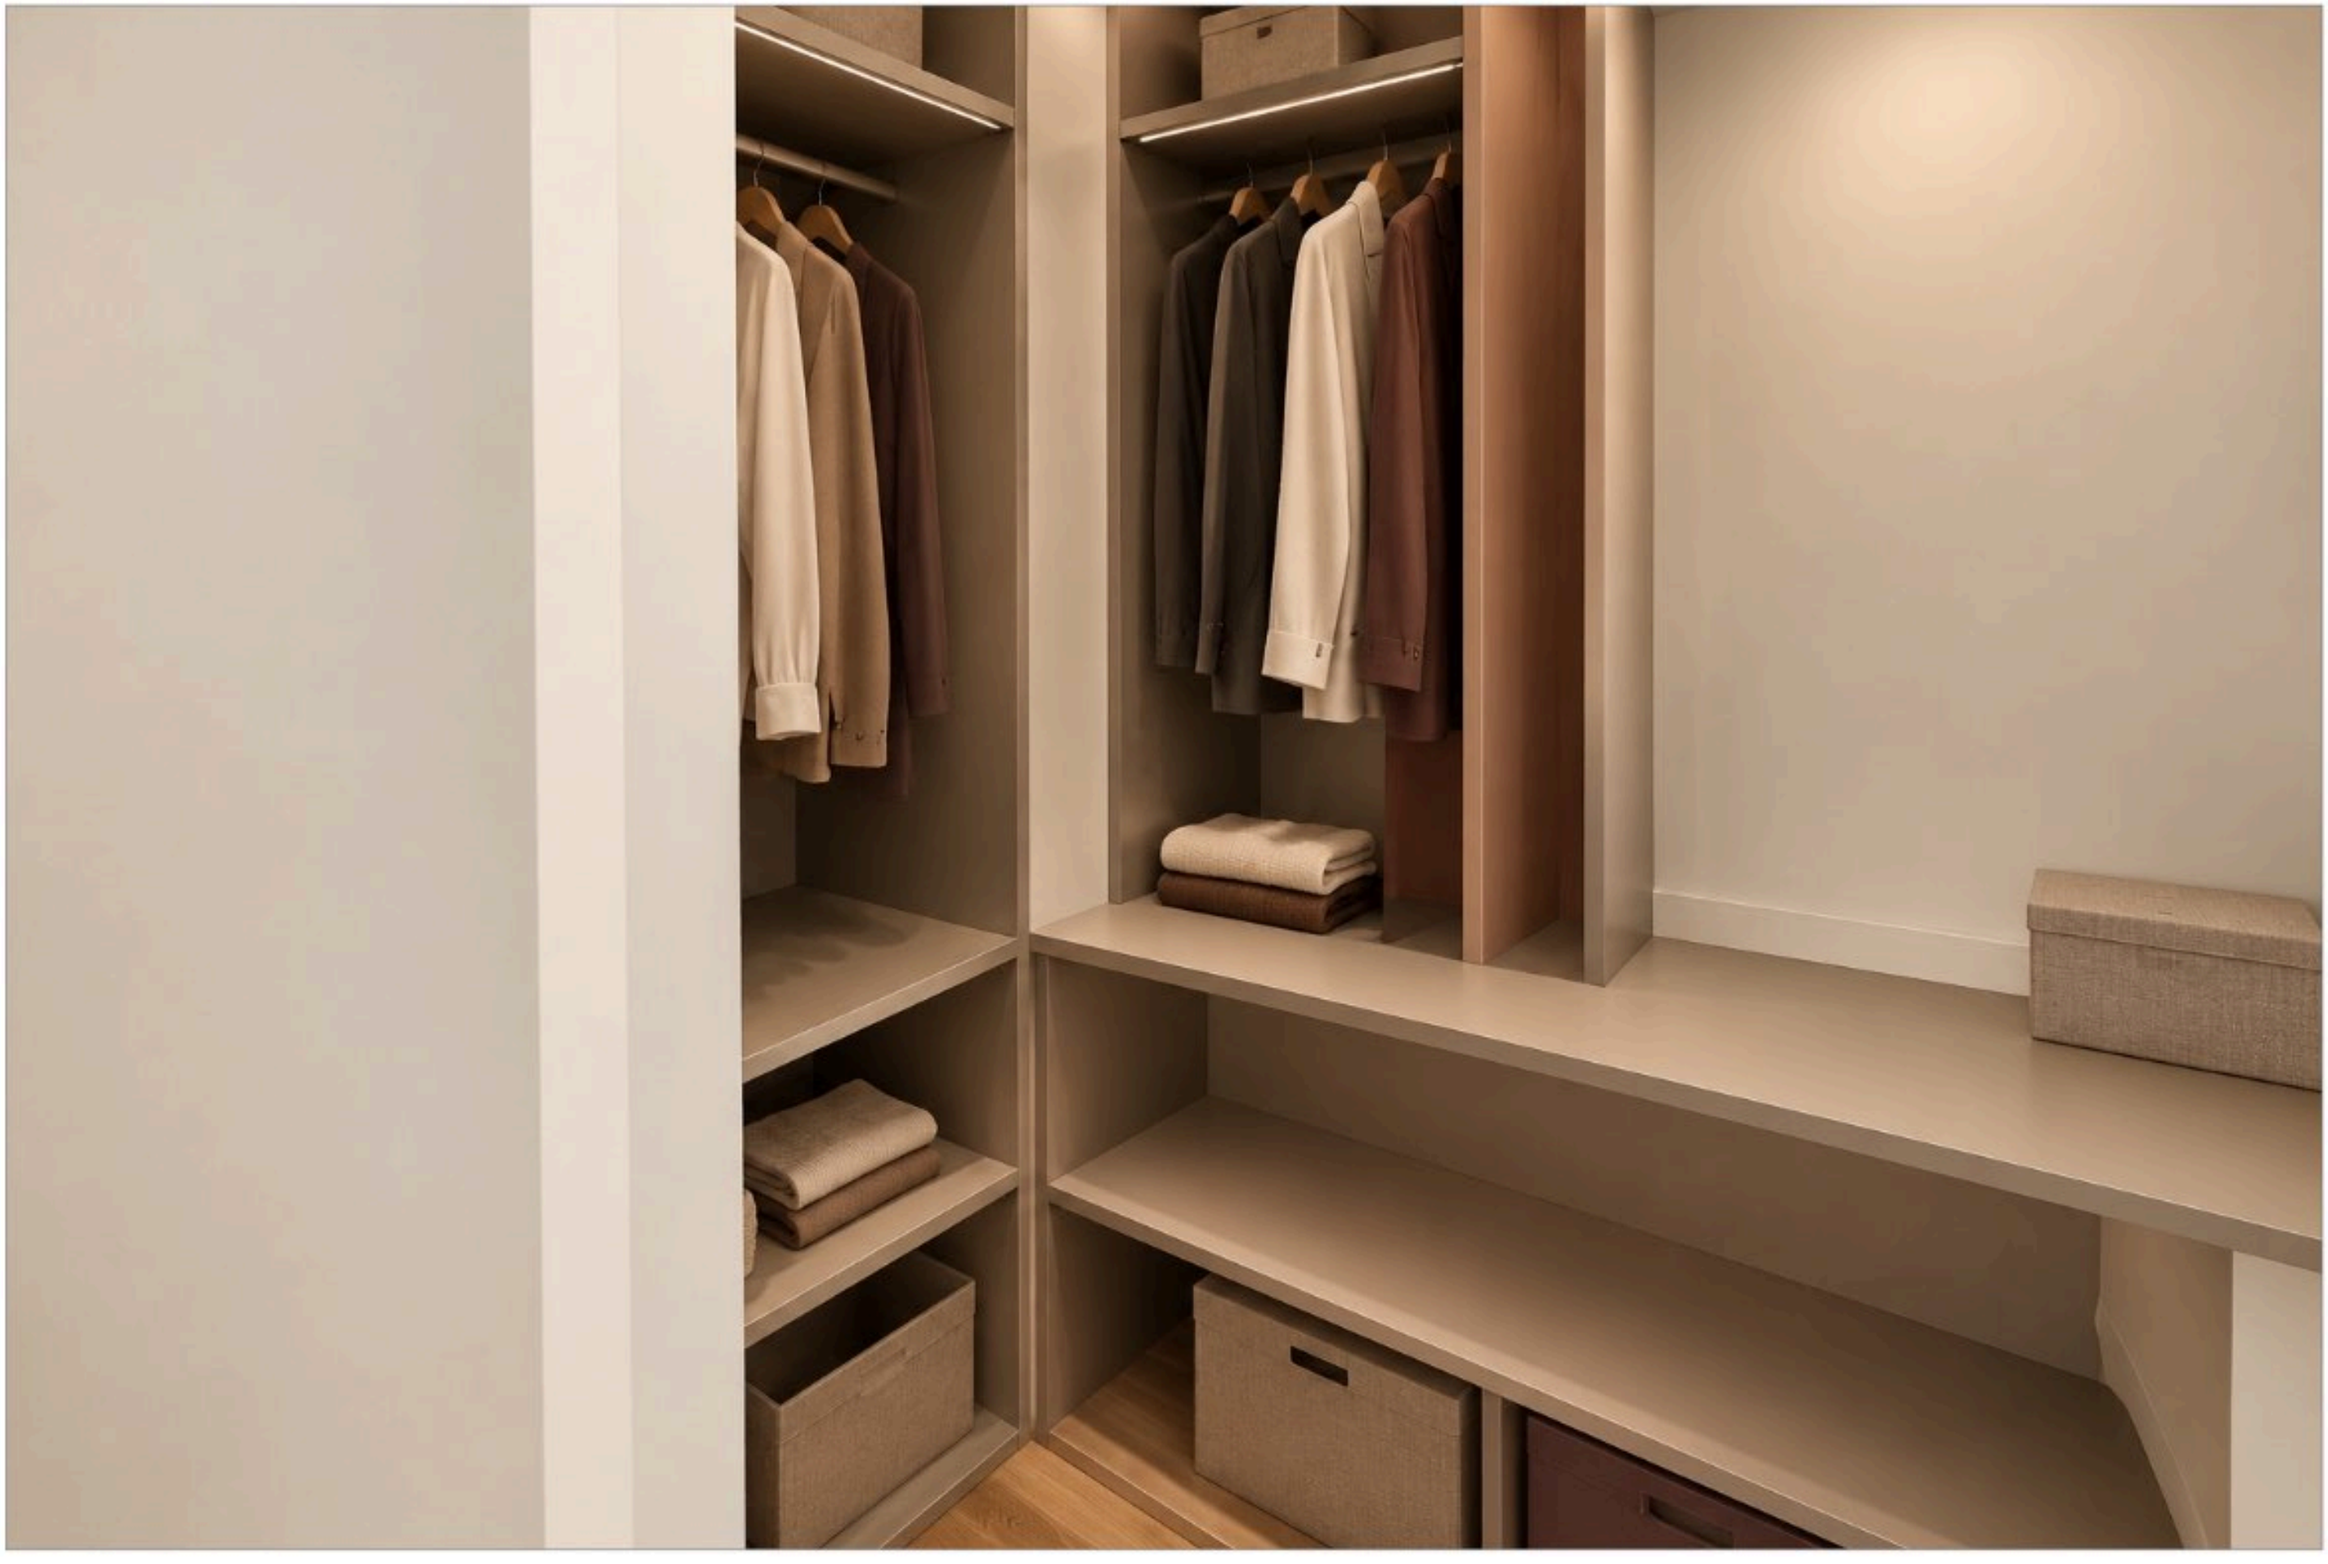


					Проект: Четырёхкомнатная квартира
	Лист	№ док.	Подпись	Дата	Визуализация: Гардеробная 2
Дизайнер	Кырпан А.С.			05.10.26	


Стадия	Лист	Листов
П	71	111

выпуск 05.10.2026 · d0efc1af8a · стр. 71 из 111

Развёртка стены А

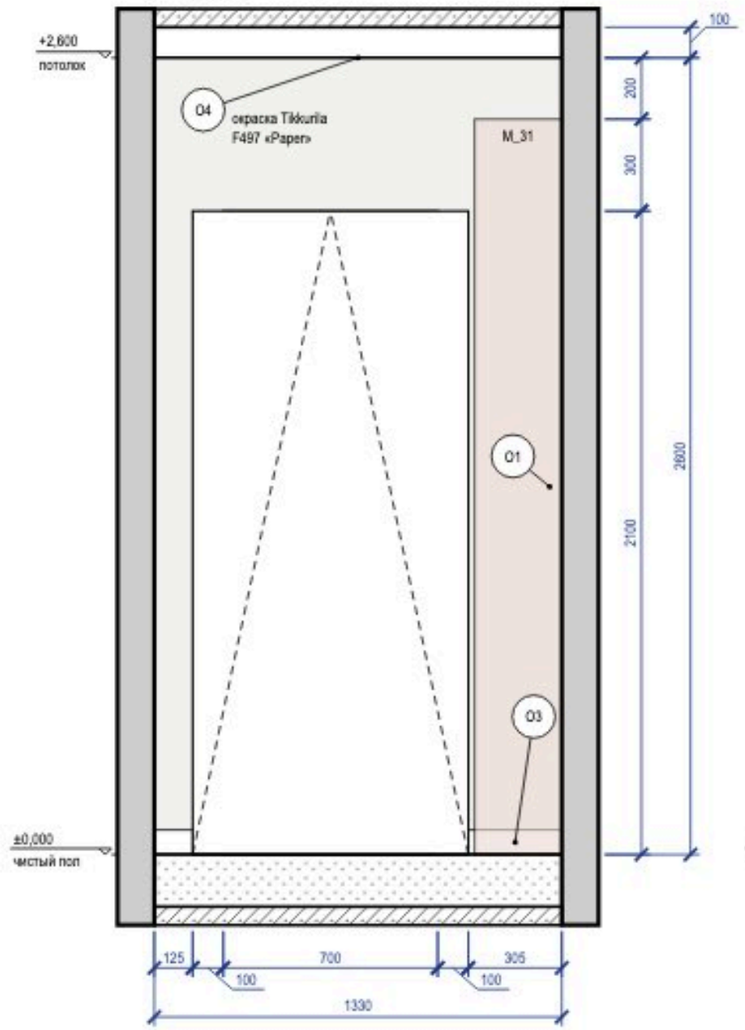

Развёртка стены Б

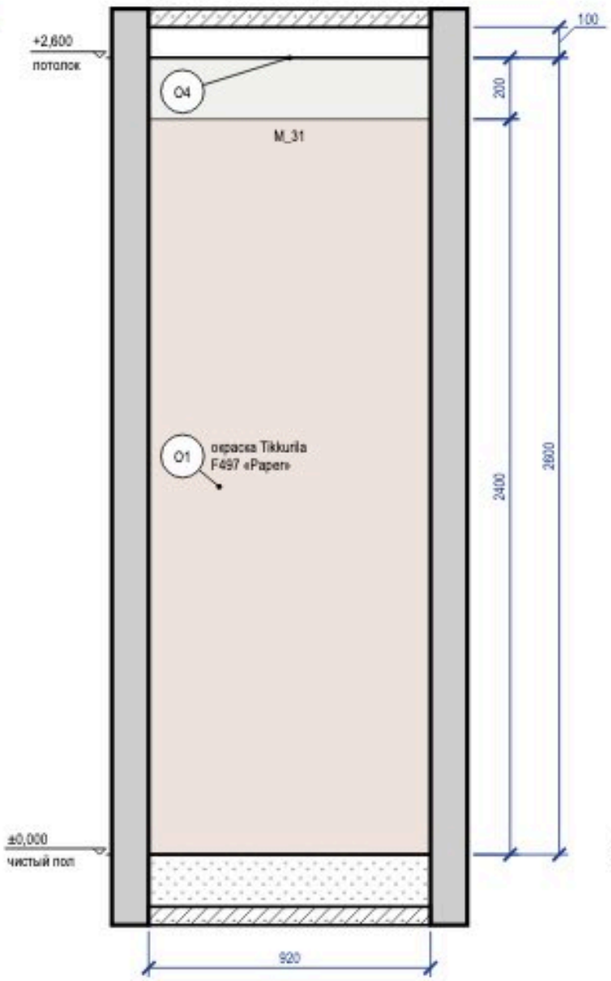

Развёртка стены В

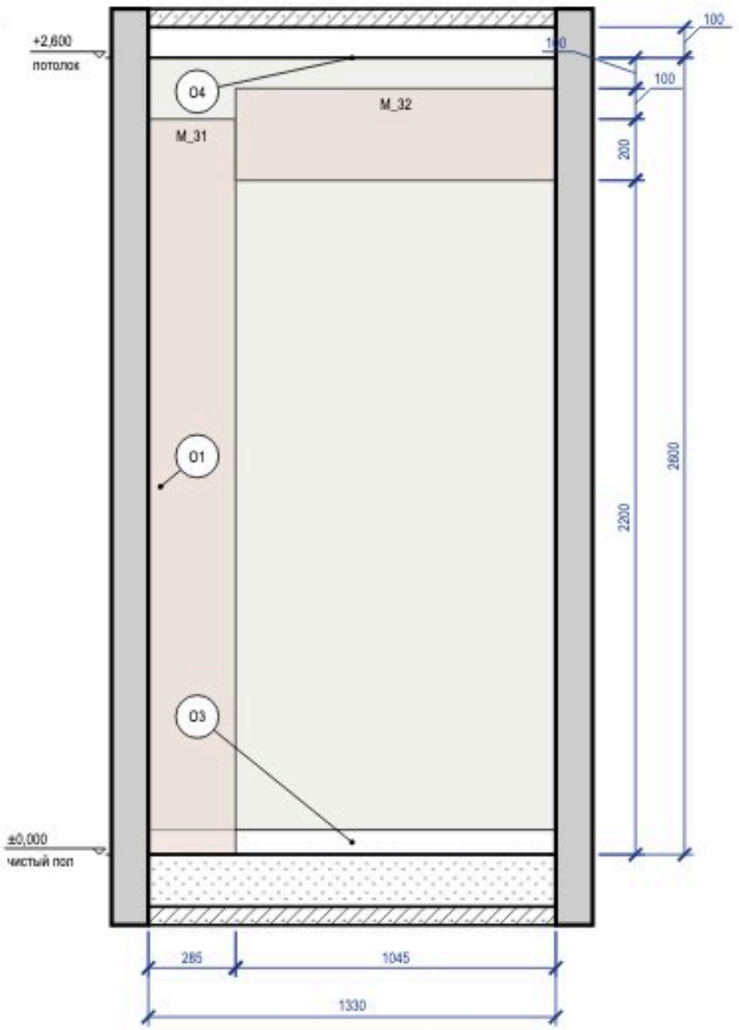


Схема развёрток (М 1:100)



Ведомость отделки (на листе)

Марка	Поверхность	Материал, изделие	Цвет, код	Кол.
О1	стены	окраска, Tikkurila Optiva 5 Matt, матовая, подготовка К3	Tikkurila F497 «Paper»	5,9 м²
О3	плинтус	плинтус МДФ, h 80 мм, аналог: плинтус МДФ под окраску 80×16 мм, полуглянцевая	Tikkurila F497 «Paper»	1,8 м
О4	потолок	окраска, Tikkurila Anti-Reflex 2, глубокоматовая, подготовка Q3	Tikkurila F497 «Paper»	1,3 м²

Визуализация этой стены — лист 71



Примечания

1. Размеры — в мм от чистовых поверхностей стен; условные обозначения и общие указания — лист 2.

					Проект: Четырёхкомнатная квартира
	Лист	№ док.	Подпись	Дата	Развёртки стен А, Б, В. Гардеробная 2 (пом. 8)
Дизайнер	Кырпан А.С.			05.10.26	

Стадия	Лист	Листов
П	72	111

выпуск 05.10.2026 · d0efc1af8a · стр. 72 из 111

Развёртка стены Г

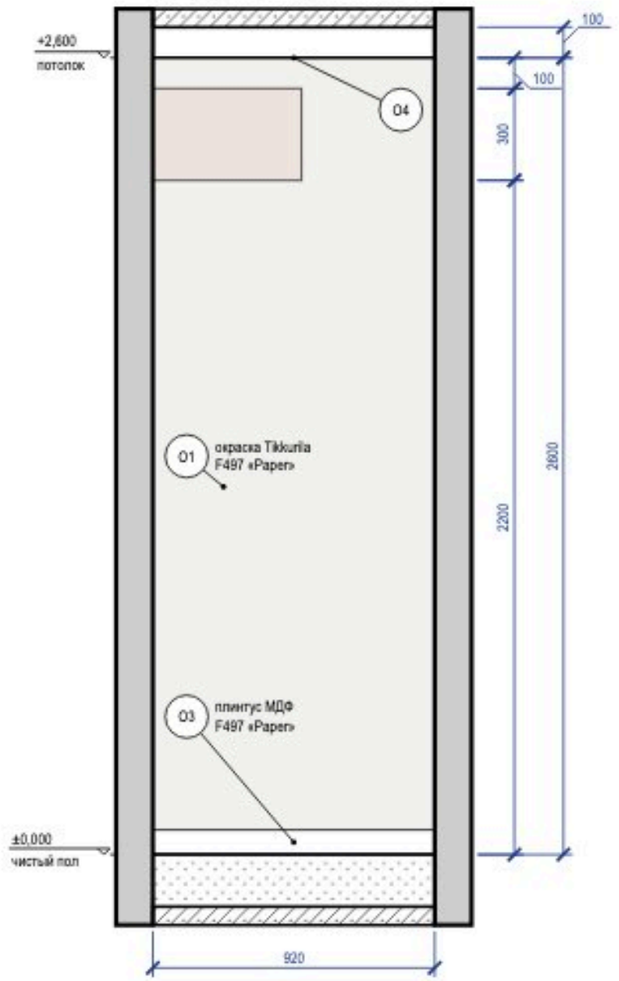


Схема развёрток (М 1:100)



Ведомость отделки (на листе)

Марка	Поверхность	Материал, изделие	Цвет, код	Кол.
О1	стены	окраска, Tikkurila Optiva 5 Matt, матовая, подготовка К3	Tikkurila F497 «Paper»	2,4 м²
О3	плинтус	плинтус МДФ, h 80 мм, аналог: плинтус МДФ под окраску 80×16 мм, полуглянцевая	Tikkurila F497 «Paper»	0,9 м
О4	потолок	окраска, Tikkurila Anti-Reflex 2, глубокоматовая, подготовка Q3	Tikkurila F497 «Paper»	1,3 м²

Примечания

1. Размеры — в мм от чистовых поверхностей стен; условные обозначения и общие указания — лист 2.

	Лист	№ док.	Подпись	Дата	Проект: Четырёхкомнатная квартира			
Дизайнер	Кырпан А.С.			05.10.26	Развёртка стены Г. Гардеробная 2 (пом. 8)	Стадия	Лист	Листов
						П	73	111

выпуск 05.10.2026 · d0efc1af8a · стр. 73 из 111



					Проект: Четырёхкомнатная квартира	
	Лист	№ док.	Подпись	Дата	Визуализация: Детская 2	Стадия / Лист / Листов
Дизайнер	Кырпан А.С.			05.10.26		П / 74 / 111

выпуск 05.10.2026 · d0efc1af8a · стр. 74 из 111



					Проект: Четырёхкомнатная квартира			
	Лист	№ док.	Подпись	Дата				
Дизайнер	Кырпан А.С.			05.10.26	Визуализация: Детская 2	Стадия	Лист	Листов
						П	75	111

выпуск 05.10.2026 № d0efc1af8a · стр. 75 из 111

Развёртка стены А

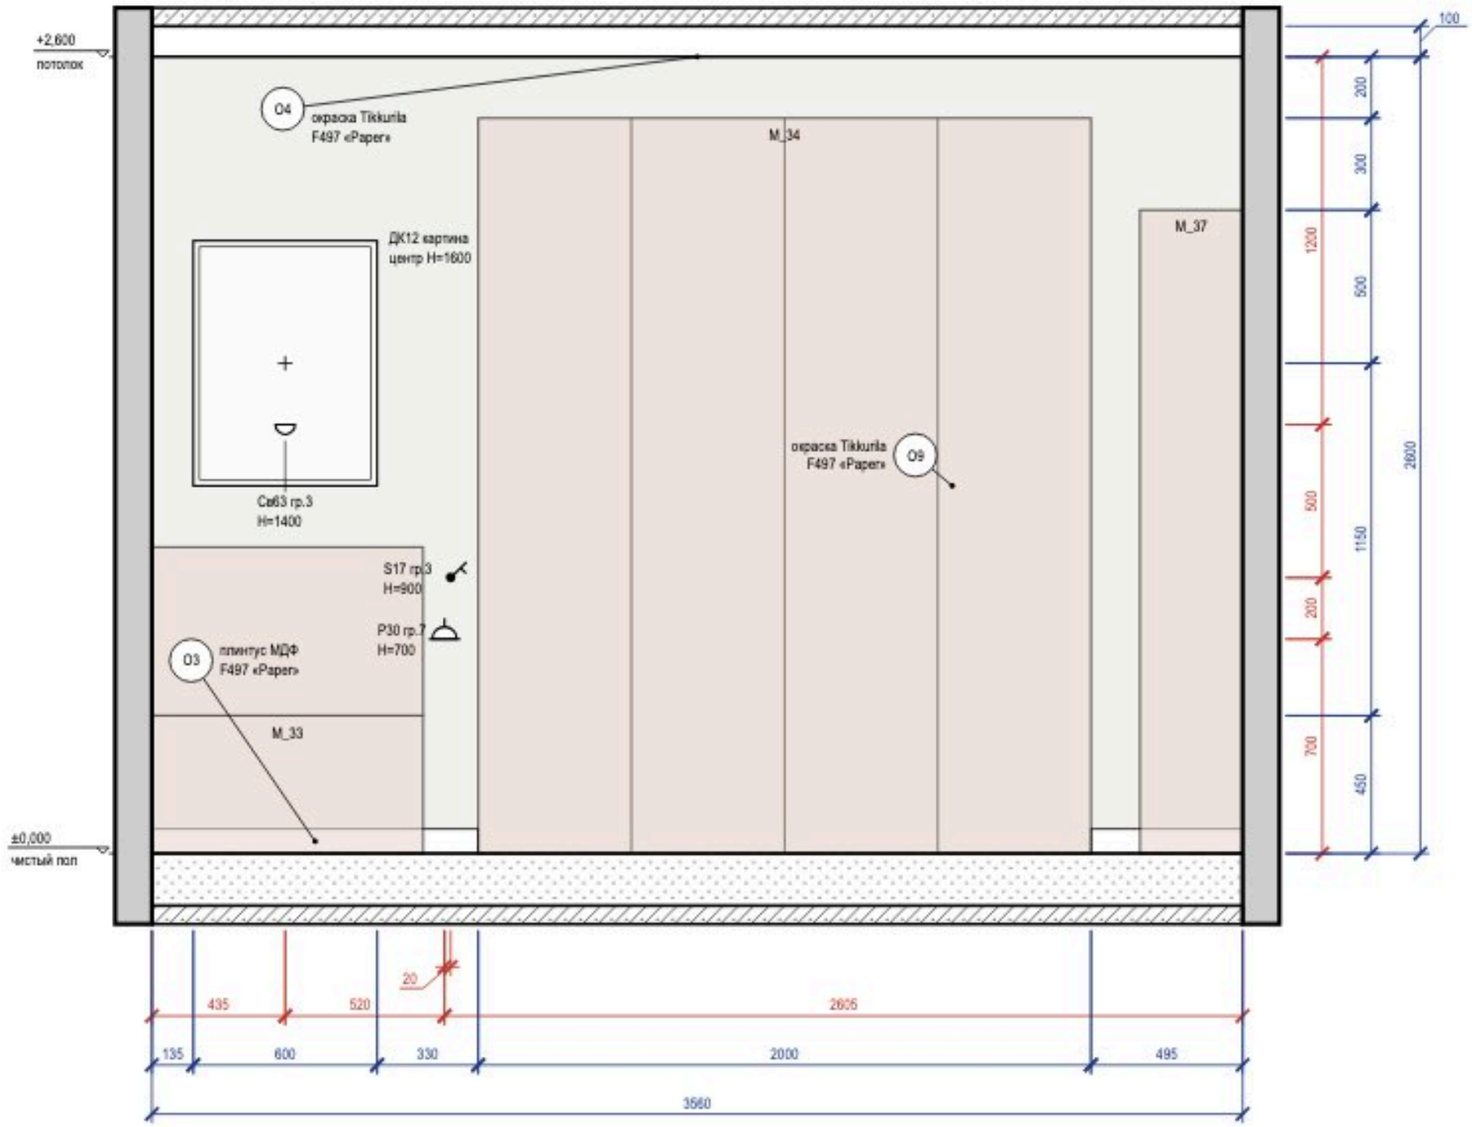



Схема развёрток (М 1:100)



Ведомость отделки (на листе)

Марка	Поверхность	Материал, изделие	Цвет, код	Кол.
О3	плинтус	плинтус МДФ, h 80 мм, аналог: плинтус МДФ под окраску 80×16 мм, полуглянцевая	Tikkurila F497 «Paper»	1,6 м
О4	потолок	окраска, Tikkurila Anti-Reflex 2, глубокоматовая, подготовка Q3	Tikkurila F497 «Paper»	11 м²
О9	стены	окраска, Tikkurila Joker, шелковисто-матовая, подготовка К3	Tikkurila F497 «Paper»	9,3 м²

Визуализация этой стены — лист 74

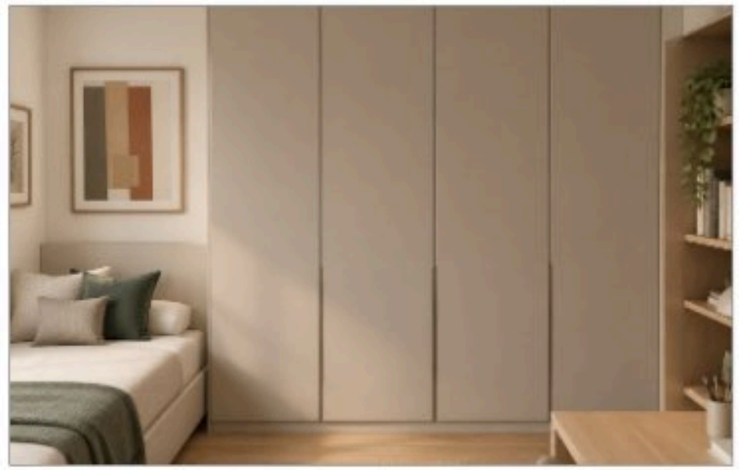

Примечания

1. Размеры — в мм от чистовых поверхностей стен; условные обозначения и общие указания — лист 2.
2. Картины и зеркала крепить к основанию по паспорту изделия (закладные и анкеры — в перечне скрытых работ); крест — ось центра предмета.

	Лист	№ док.	Подпись	Дата	Проект: Четырёхкомнатная квартира			
Дизайнер	Кырпан А.С.			05.10.26	Развёртка стены А. Детская 2 (пом. 9)	Стадия	Лист	Листов
						П	76	111

выпуск 05.10.2026 · d0efc1af8a · стр. 76 из 111

Развёртка стены Б

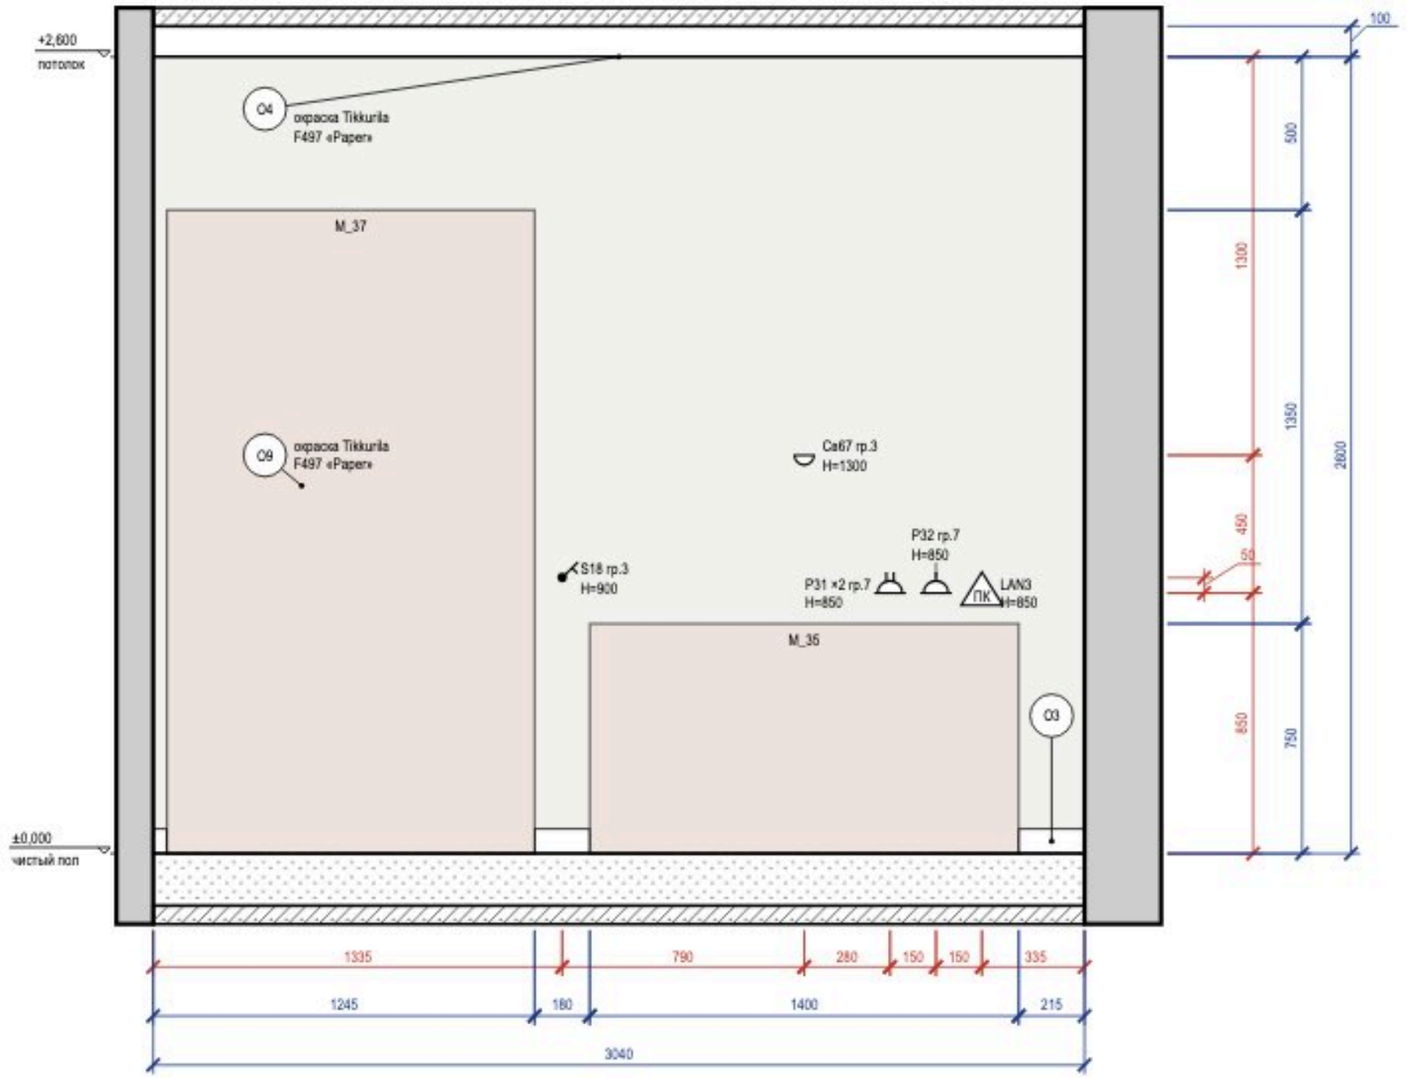


Схема развёрток (М 1:100)



Ведомость отделки (на листе)

Марка	Поверхность	Материал, изделие	Цвет, код	Кол.
О3	плинтус	плинтус МДФ, h 80 мм, аналог: плинтус МДФ под окраску 80×16 мм, полуглянцевая	Tikkurila F497 «Paper»	0,4 м
О4	потолок	окраска, Tikkurila Anti-Reflex 2, глубокоматовая, подготовка Q3	Tikkurila F497 «Paper»	11 м²
О9	стены	окраска, Tikkurila Joker, шелковисто-матовая, подготовка К3	Tikkurila F497 «Paper»	7,9 м²

Примечания

1. Размеры — в мм от чистовых поверхностей стен; условные обозначения и общие указания — лист 2.

					Проект: Четырёхкомнатная квартира
	Лист	№ док.	Подпись	Дата	Развёртка стены Б. Детская 2 (пом. 9)
Дизайнер	Кырпан А.С.			05.10.26	

Стадия	Лист	Листов
П	77	111

выпуск 05.10.2026 · d0efc1af8a · стр. 77 из 111

Развёртка стены В

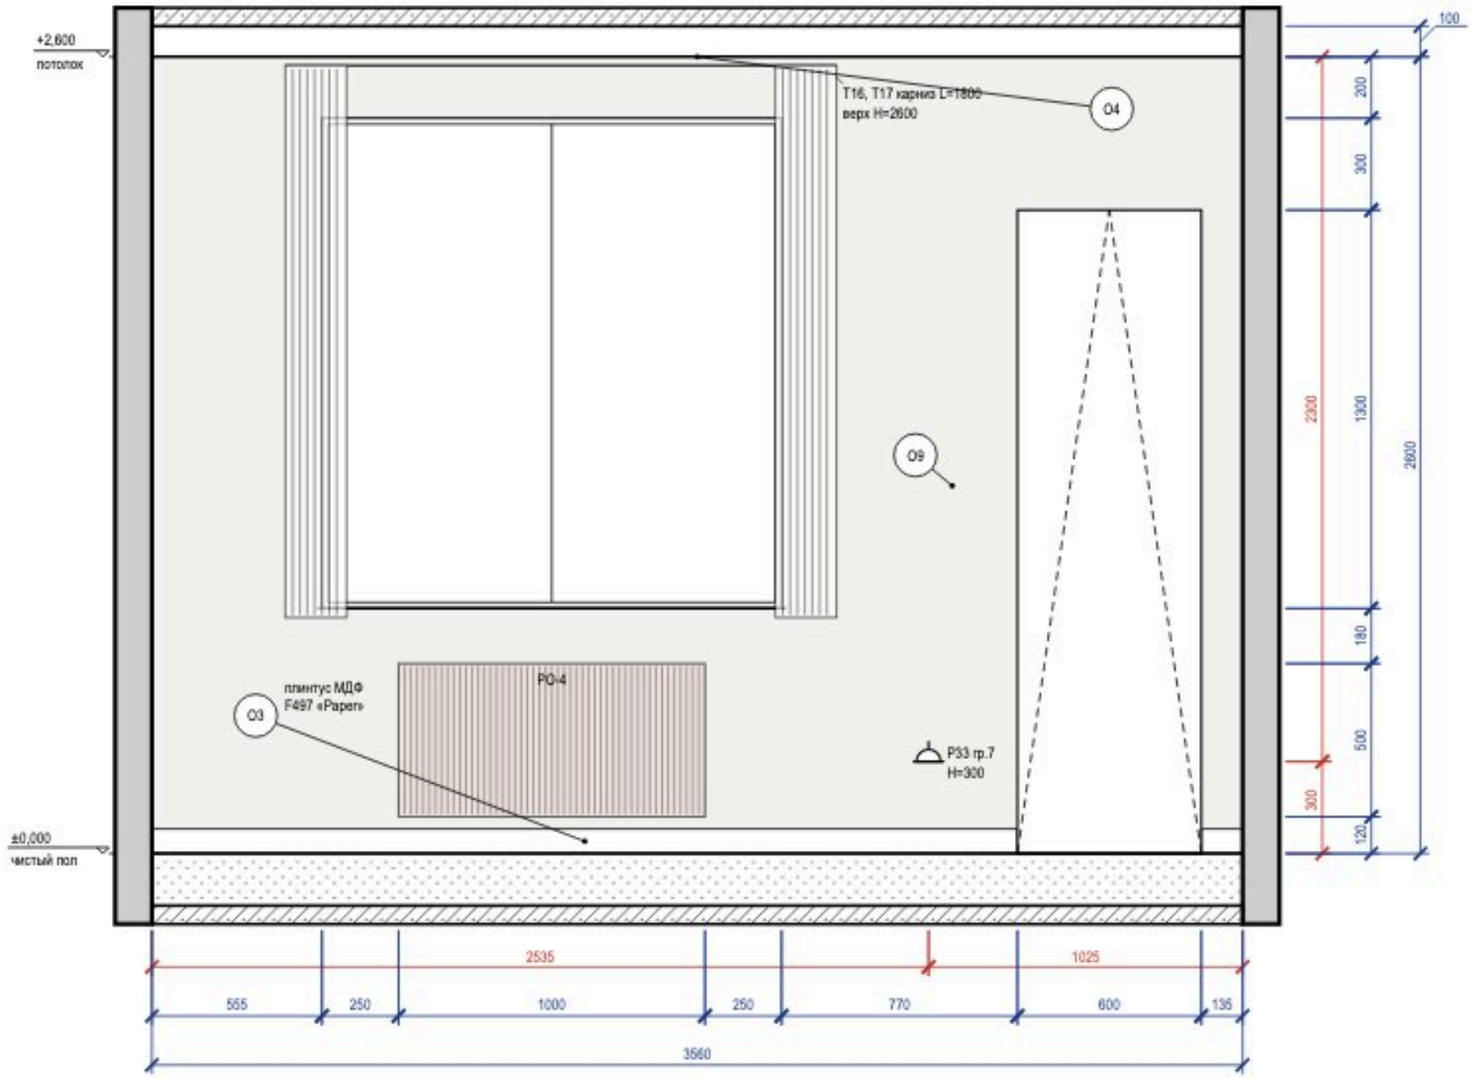


Схема развёрток (М 1:100)



Ведомость отделки (на листе)

Марка	Поверхность	Материал, изделие	Цвет, код	Кол.
О3	плинтус	плинтус МДФ, h 80 мм, аналог: плинтус МДФ под окраску 80×16 мм, полуглянцевая	Tikkurila F497 «Paperi»	3 м
О4	потолок	окраска, Tikkurila Anti-Reflex 2, глубокоматовая, подготовка Q3	Tikkurila F497 «Paperi»	11 м²
О9	стены	окраска, Tikkurila Joker, шелковисто-матовая, подготовка К3	Tikkurila F497 «Paperi»	5,6 м²

Примечания

1. Размеры — в мм от чистовых поверхностей стен; условные обозначения и общие указания — лист 2.
2. Карнизы (шины) — по ведомости текстиля декоратора; длина L и верх H — по развёртке, крепление — до окраски потолка.

					Проект: Четырёхкомнатная квартира
	Лист	№ док.	Подпись	Дата	Развёртка стены В. Детская 2 (пом. 9)
Дизайнер	Кырпан А.С.			05.10.26	

Стадия	Лист	Листов
П	78	111

выпуск 05.10.2026 № d0efc1af8a · стр. 78 из 111

Развёртка стены Г

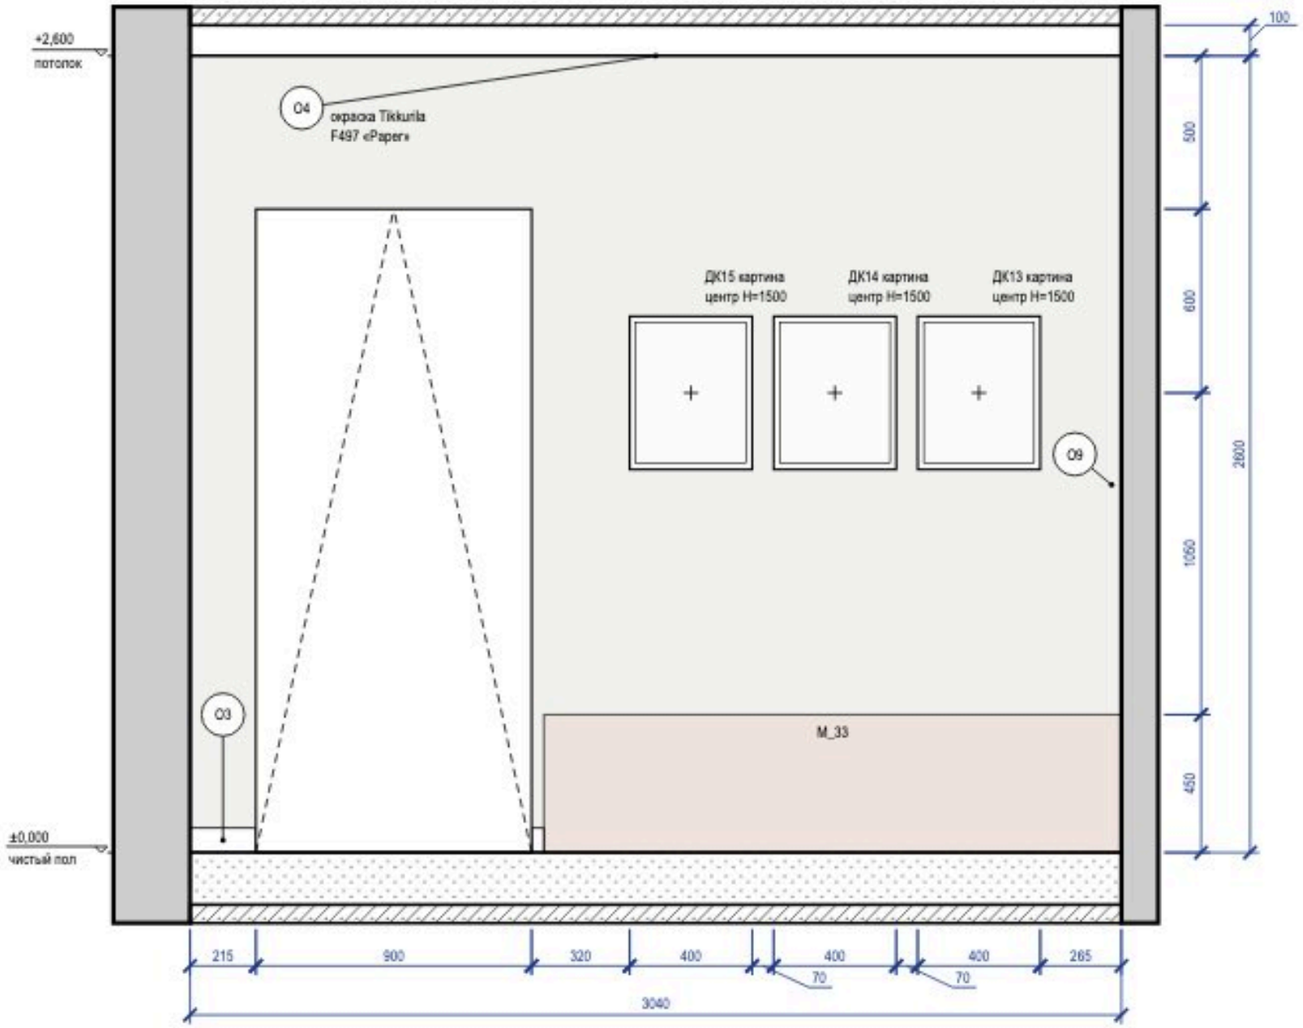



Схема развёрток (М 1:100)



Ведомость отделки (на листе)

Марка	Поверхность	Материал, изделие	Цвет, код	Кол.
О3	плинтус	плинтус МДФ, h 80 мм, аналог: плинтус МДФ под окраску 80×16 мм, полуглянцевая	Tikkurila F497 «Paper»	0,3 м
О4	потолок	окраска, Tikkurila Anti-Reflex 2, глубокоматовая, подготовка Q3	Tikkurila F497 «Paper»	11 м²
О9	стены	окраска, Tikkurila Joker, шелковисто-матовая, подготовка К3	Tikkurila F497 «Paper»	6 м²

Визуализация этой стены — лист 75

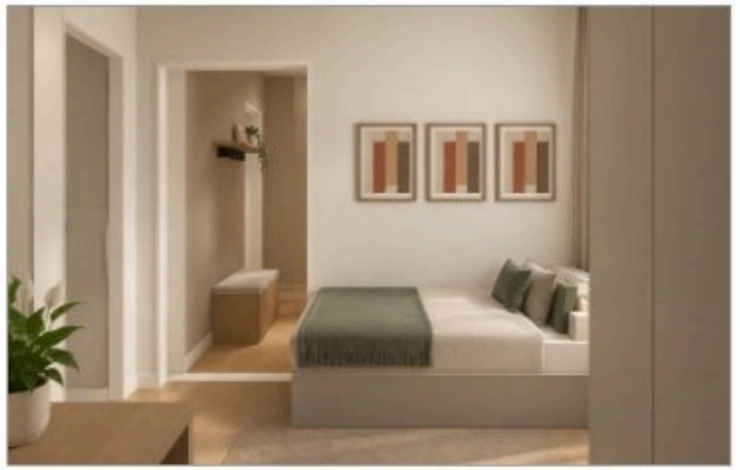

Примечания

1. Размеры — в мм от чистовых поверхностей стен; условные обозначения и общие указания — лист 2.
2. Картины и зеркала крепить к основанию по паспорту изделия (закладные и анкеры — в перечне скрытых работ); крест — ось центра предмета.

					Проект: Четырёхкомнатная квартира
	Лист	№ док.	Подпись	Дата	
Дизайнер	Кырпан А.С.			05.10.26	Развёртка стены Г. Детская 2 (пом. 9)

Стадия	Лист	Листов
П	79	111


выпуск 05.10.2026 · d0efc1af8a · стр. 79 из 111



					Проект: Четырёхкомнатная квартира	
	Лист	№ док.	Подпись	Дата		
Дизайнер	Кырпан А.С.			05.10.26	Визуализация санузла	Стадия: П; Лист: 80; Листов: 111

выпуск 05.10.2026 № d0efc1af8a · стр. 80 из 111

Развёртка стены А

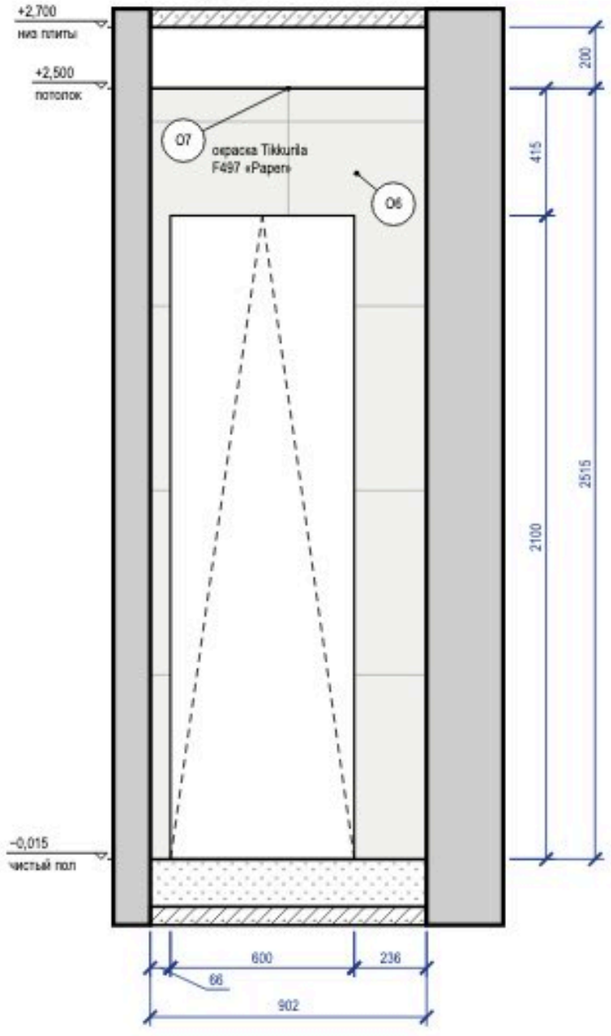

Развёртка стены Б

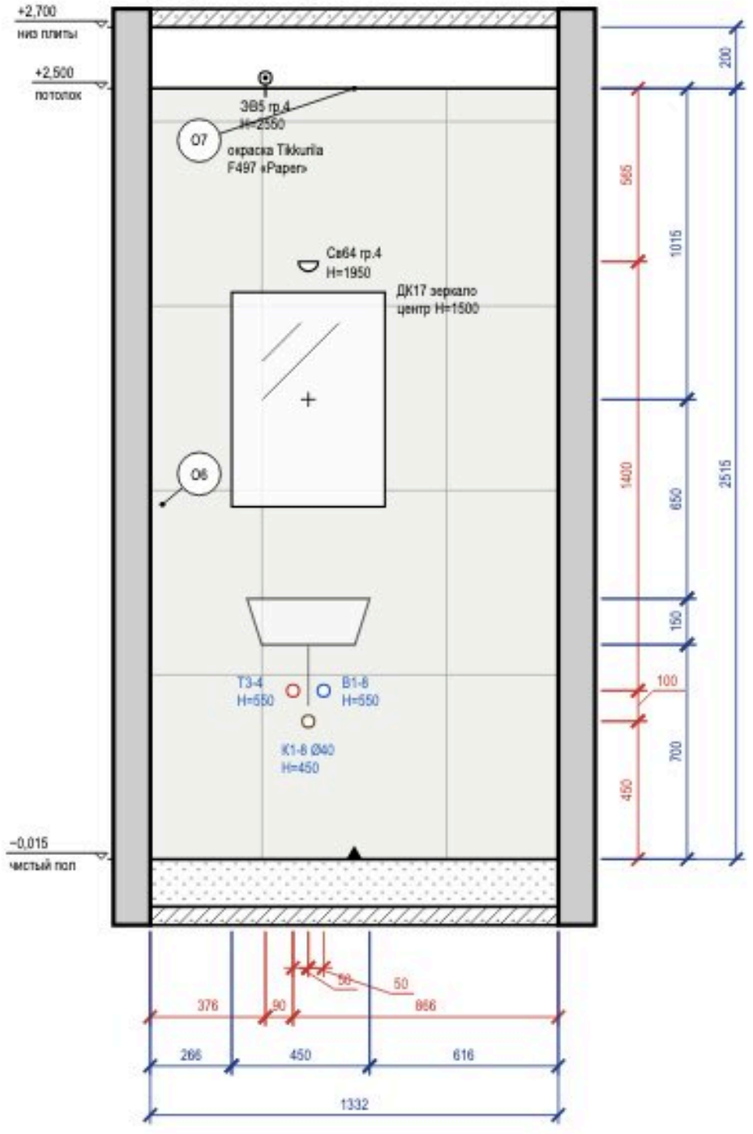


Схема развёрток (М 1:100)



Ведомость отделки (на листе)

Марка	Поверхность	Материал, изделие	Цвет, код	Кол.
О6	стены	облицовка плиткой, 600×600×9 мм, аналог: керамогранит матовый, тон F497, затирка CG2WA	#F1F1EC «тон Paper F497»	4,4 м²
О7	потолок	окраска, Tikkurila Luja 7, матовая, подготовка Q3	Tikkurila F497 «Paper»	1,3 м²


Примечания

1. Размеры — в мм от чистовых поверхностей стен; условные обозначения и общие указания — лист 2.
2. Облицовка — по сетке швов 2 мм, раскладка от оси стены (треугольник у пола); подрезки — по листу раскладки плитки.
3. Гидроизоляция в 2 слоя, заход на стены 200 мм — до облицовки, с актом скрытых работ и тестом проливом (узел — на листе узлов).
4. Картины и зеркала крепить к основанию по паспорту изделия (закладные и анкеры — в перечне скрытых работ); крест — ось центра предмета.
5. Линии узора (швы плитки, складки штор, рёбра радиаторов) прерываются у знаков и выносок — просвет между линиями не менее 0,7 мм.

					Проект: Четырёхкомнатная квартира			
	Лист	№ док.	Подпись	Дата	Развёртки стен А, Б. Санузел (пом. 10)	Стадия	Лист	Листов
Дизайнер	Кырпан А.С.			05.10.26		П	81	111

выпуск 05.10.2026 · d0efc1af8a · стр. 81 из 111

Развёртка стены В

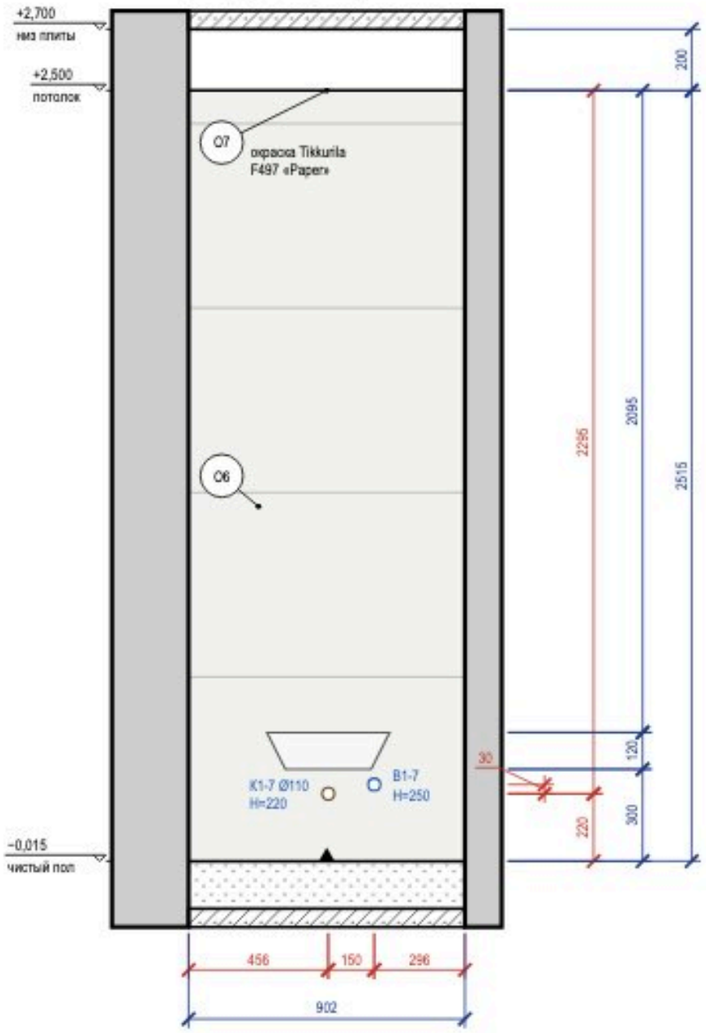

Развёртка стены Г

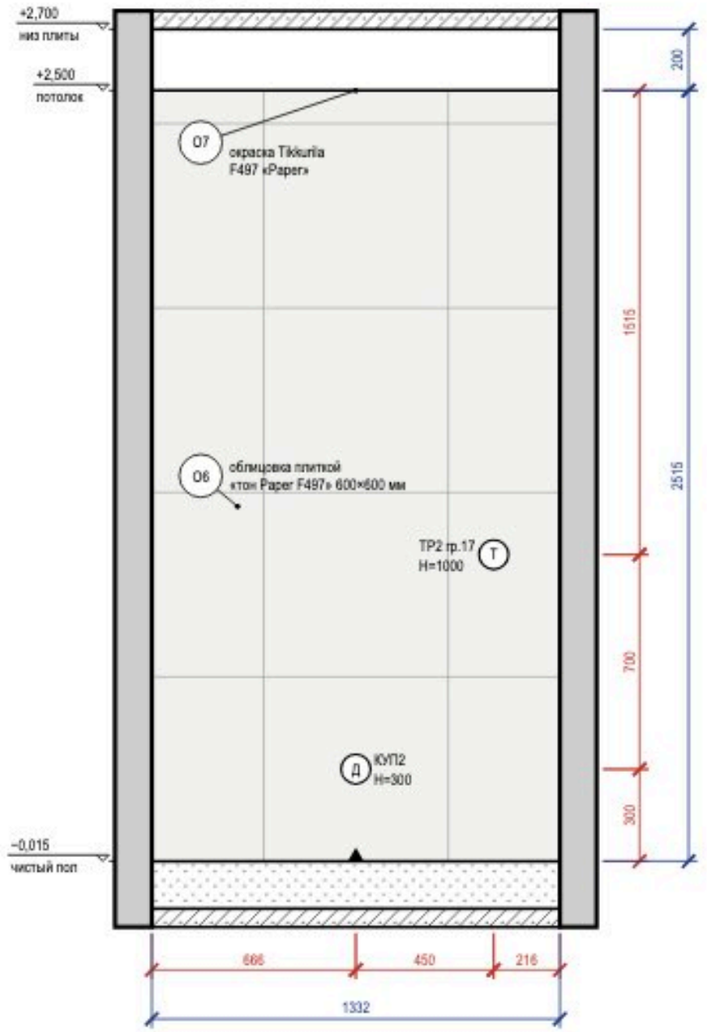



Схема развёрток (М 1:100)



Ведомость отделки (на листе)

Марка	Поверхность	Материал, изделие	Цвет, код	Кол.
О6	стены	облицовка плиткой, 600×600×9 мм, аналог: керамогранит матовый, тон F497, затирка CG2WA	#F1F1EC «тон Paper F497»	5,6 м²
О7	потолок	окраска, Tikkurila Luja 7, матовая, подготовка Q3	Tikkurila F497 «Paper»	1,3 м²

Визуализация этой стены — лист 80

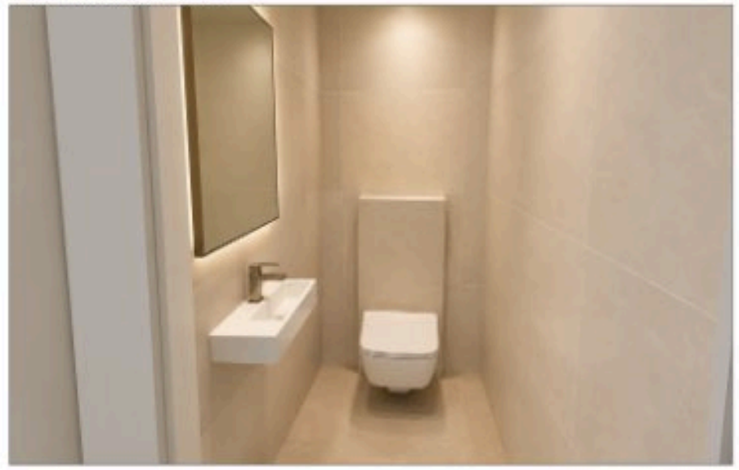

Примечания

1. Размеры — в мм от чистовых поверхностей стен; условные обозначения и общие указания — лист 2.
2. Облицовка — по сетке швов 2 мм, раскладка от оси стены (треугольник у пола); подрезки — по листу раскладки плитки.
3. Гидроизоляция в 2 слоя, заход на стены 200 мм — до облицовки, с актом скрытых работ и тестом проливом (узел — на листе узлов).

					Проект: Четырёхкомнатная квартира			
	Лист	№ док.	Подпись	Дата	Развёртки стен В, Г. Санузел (пом. 10)	Стадия	Лист	Листов
Дизайнер	Кырпан А.С.			05.10.26		П	82	111

выпуск 05.10.2026 · d0efc1af8a · стр. 82 из 111



					Проект: Четырёхкомнатная квартира	
	Лист	№ док.	Подпись	Дата		
Дизайнер	Кырпан А.С.			05.10.26	Визуализация гостиной	Стадия: П; Лист: 83; Листов: 111

выпуск 05.10.2026 · d0efc1af8a · стр. 83 из 111



					Проект: Четырёхкомнатная квартира	
	Лист	№ док.	Подпись	Дата		
Дизайнер	Кырпан А.С.			05.10.26	Визуализация гостиной	Стадия: П; Лист: 84; Листов: 111

выпуск 05.10.2026 · d0efc1af8a · стр. 84 из 111

Развёртка стены А


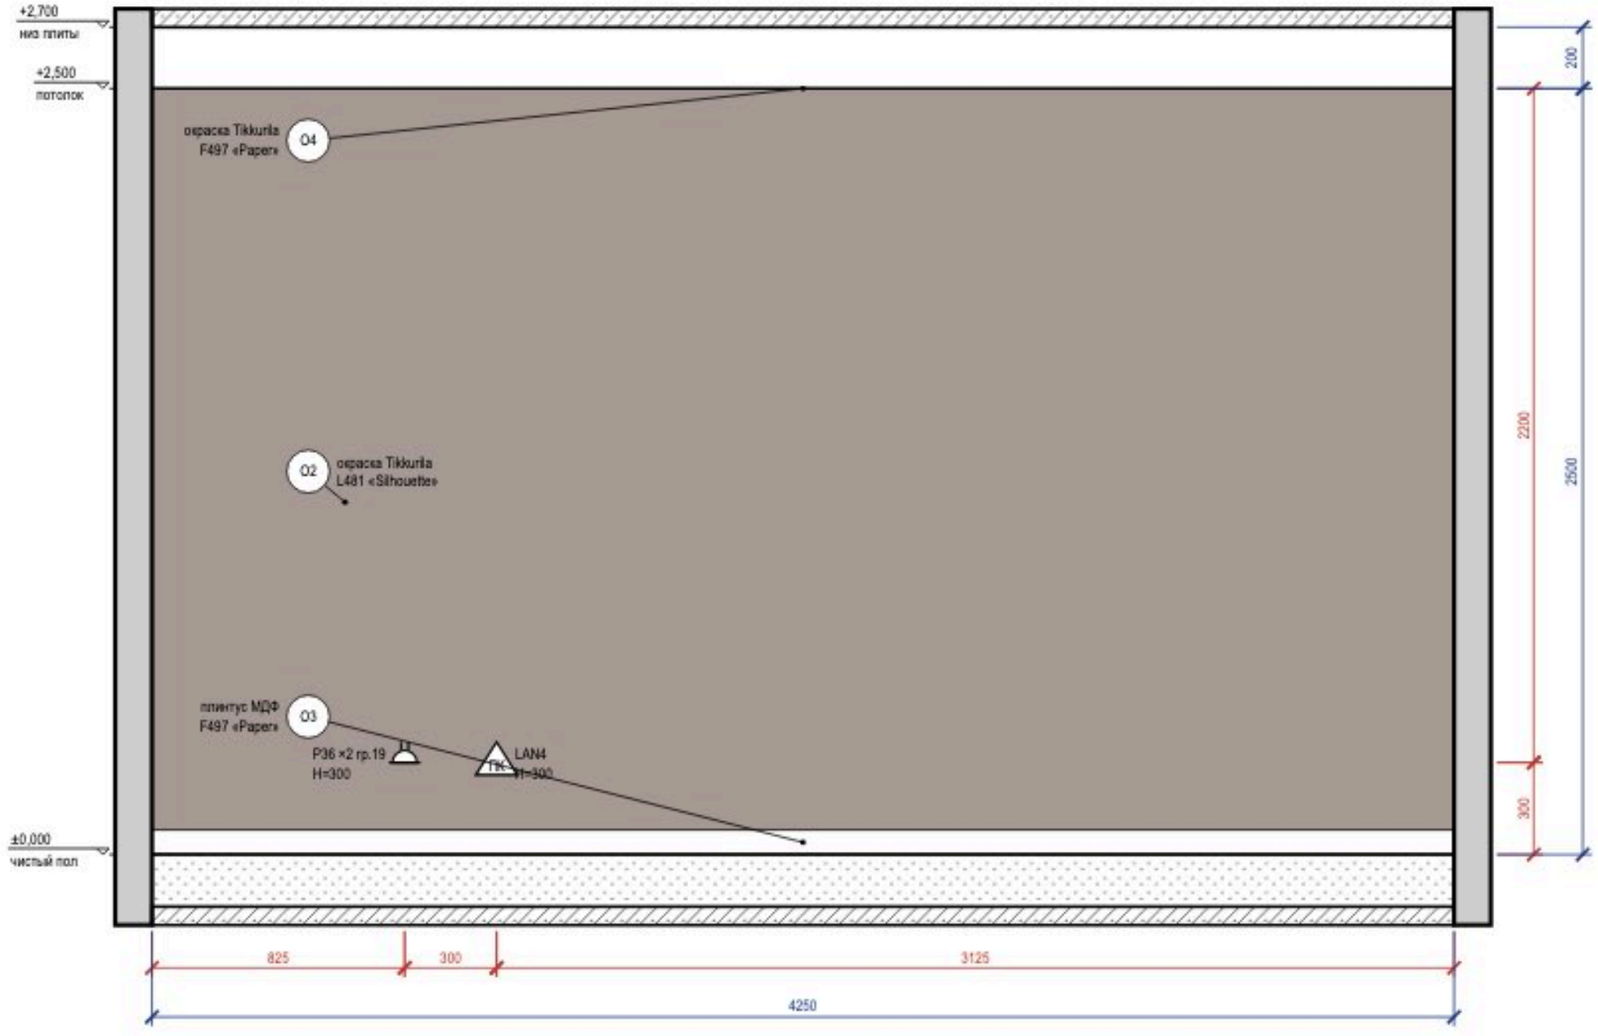



Схема развёрток (М 1:100)

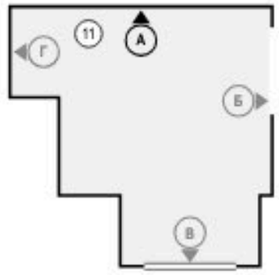

Ведомость отделки (на листе)

Марка	Поверхность	Материал, изделие	Цвет, код	Кол.
О2	акцентная стена	окраска, Tikkurila Optiva 5 Matt, аналог: интерьерная краска, класс 2 по EN 13300, глубокоматовая/матовая, база С, матовая, подготовка К3	Tikkurila L481 «Silhouette»	10,6 м²
О3	плинтус	плинтус МДФ, h 80 мм, аналог: плинтус МДФ под окраску 80×16 мм, полуглянцевая	Tikkurila F497 «Paper»	4,3 м
О4	потолок	окраска, Tikkurila Anti-Reflex 2, глубокоматовая, подготовка О3	Tikkurila F497 «Paper»	14,6 м²

Визуализация этой стены — лист 83

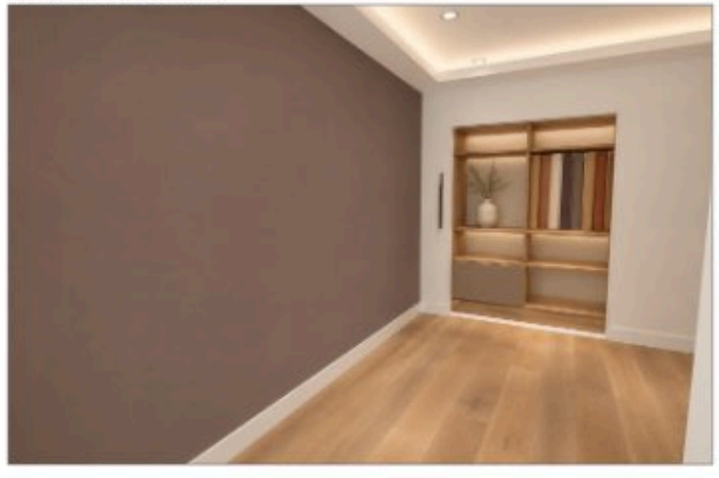

Примечания

1. Размеры — в мм от чистовых поверхностей стен; условные обозначения и общие указания — лист 2.
2. Потолок на развёртках — по нижнему уровню У1; другие уровни потолка помещения: У2 +2,600.

					Проект: Четырёхкомнатная квартира
	Лист	№ док.	Подпись	Дата	Развёртка стены А. Гостиная (пом. 11)
Дизайнер	Кырпан А.С.			05.10.26	

Стадия	Лист	Листов
П	85	111

выпуск 05.10.2026 · d0efc1af8a · стр. 85 из 111

Развёртка стены Б


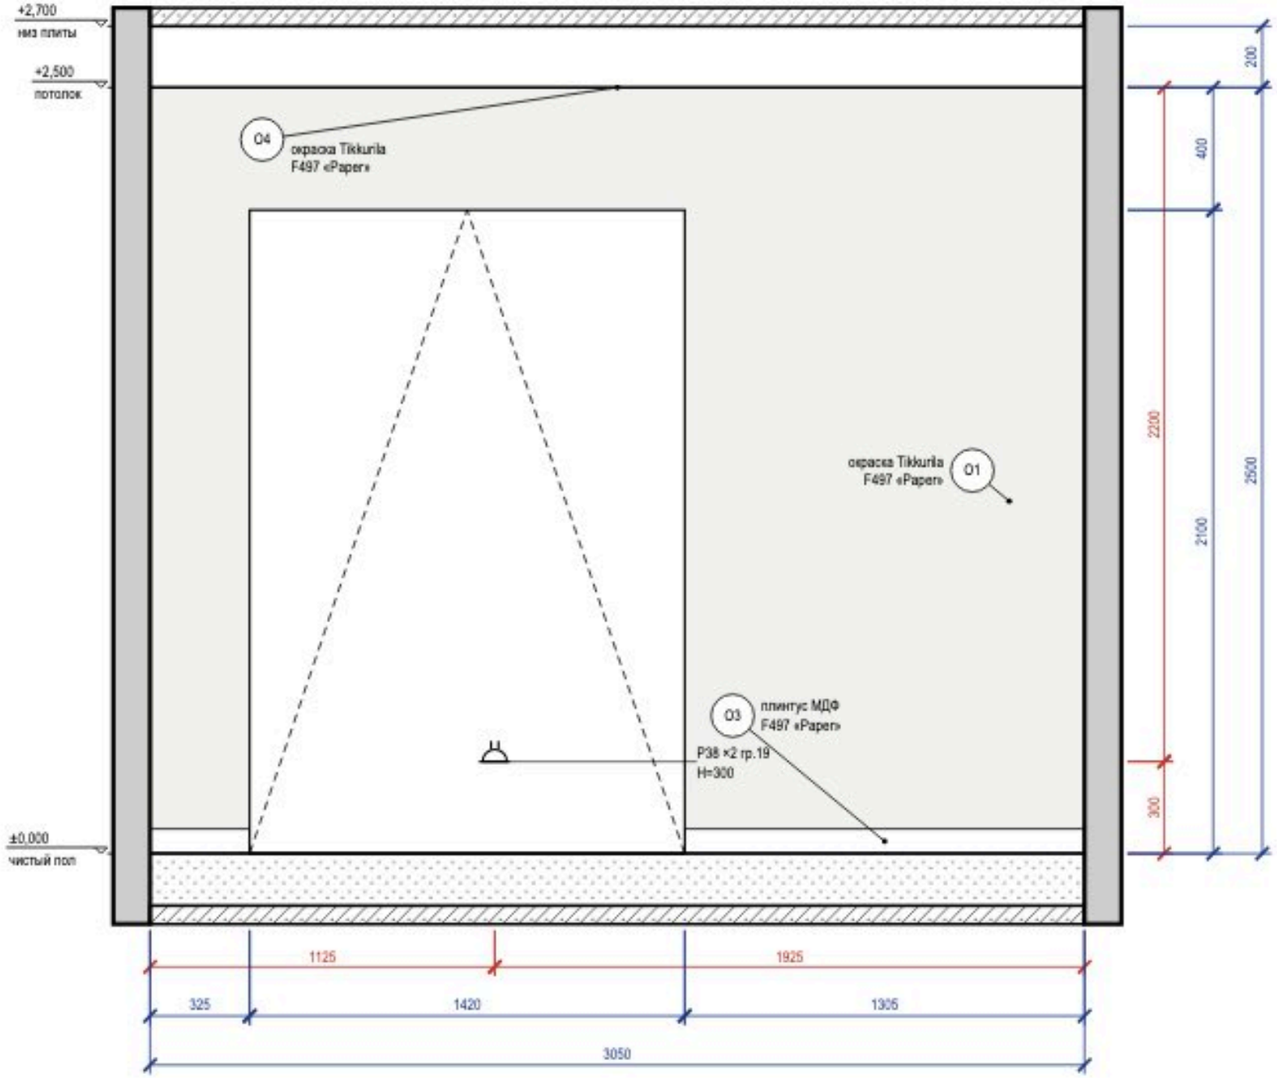


Схема развёрток (М 1:100)

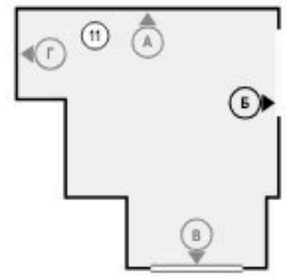

Ведомость отделки (на листе)

Марка	Поверхность	Материал, изделие	Цвет, код	Кол.
О1	стены	окраска, Tikkurila Optiva 5 Matt, матовая, подготовка К3	Tikkurila F497 «Paper»	4,6 м²
О3	плинтус	плинтус МДФ, h 80 мм, аналог: плинтус МДФ под окраску 80×16 мм, полуглянцевая	Tikkurila F497 «Paper»	1,6 м
О4	потолок	окраска, Tikkurila Anti-Reflex 2, глубокоматовая, подготовка Q3	Tikkurila F497 «Paper»	14,6 м²

Визуализация этой стены — лист 84



Примечания


1. Размеры — в мм от чистовых поверхностей стен; условные обозначения и общие указания — лист 2.
2. Потолок на развёртках — по нижнему уровню У1; другие уровни потолка помещения: У2 +2,600.

					Проект: Четырёхкомнатная квартира
	Лист	№ док.	Подпись	Дата	Развёртка стены Б. Гостиная (пом. 11)
Дизайнер	Кырпан А.С.			05.10.26	

Стадия	Лист	Листов
П	86	111

выпуск 05.10.2026 № d0efc1af8a · стр. 86 из 111

Развёртка стены В

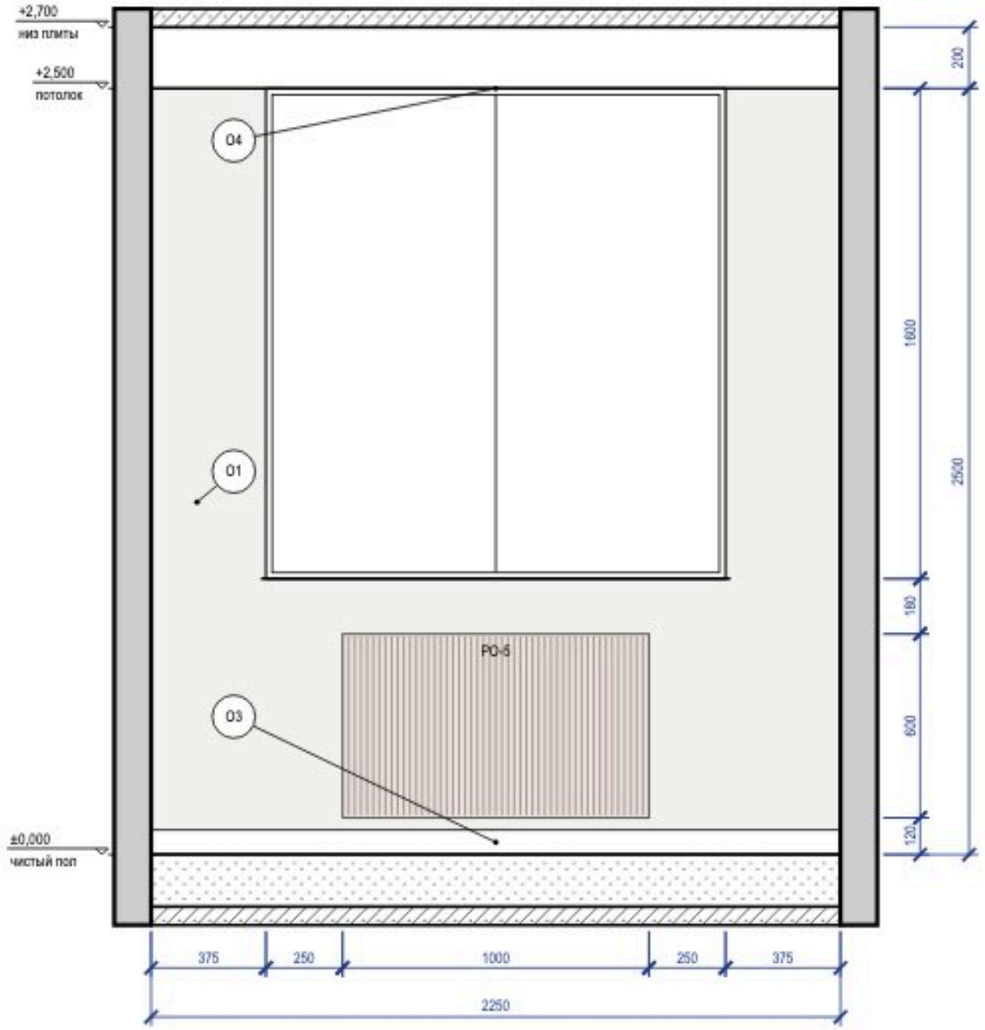

Развёртка стены Г


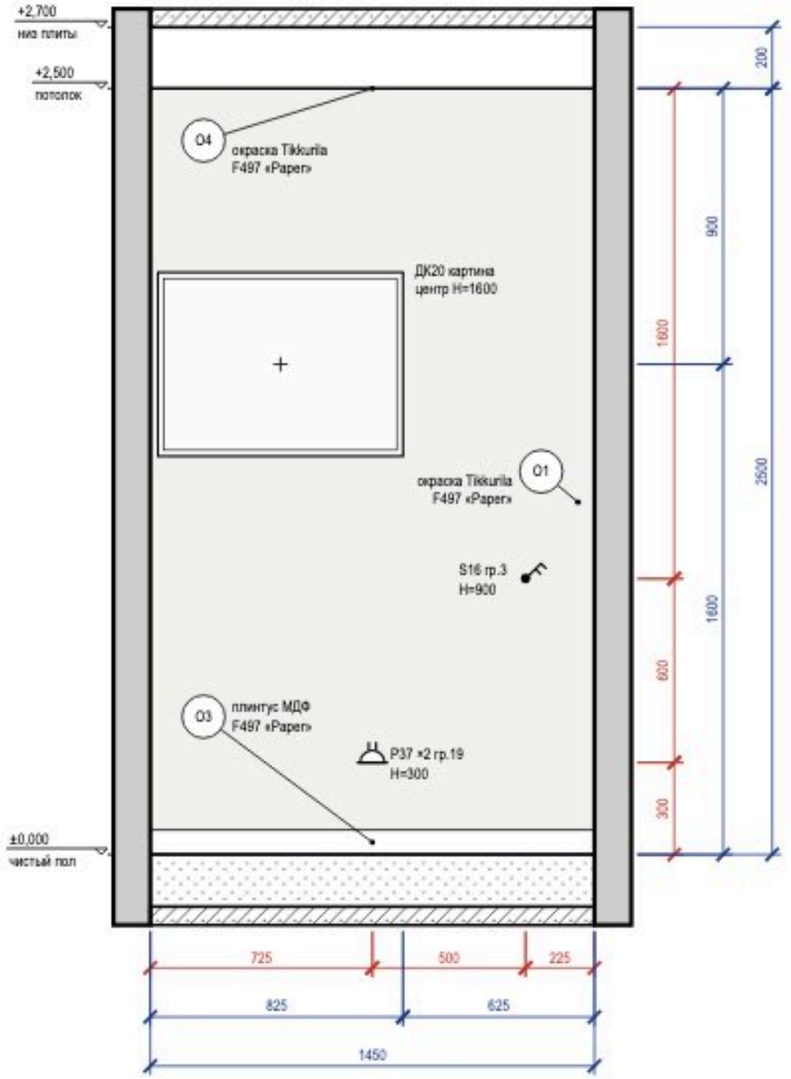


Схема развёрток (М 1:100)

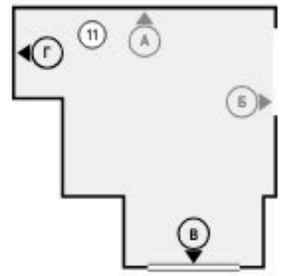

Ведомость отделки (на листе)

Марка	Поверхность	Материал, изделие	Цвет, код	Кол.
О1	стены	окраска, Tikkurila Optiva 5 Matt, матовая, подготовка К3	Tikkurila F497 «Paper»	6,8 м²
О3	плинтус	плинтус МДФ, h 80 мм, аналог: плинтус МДФ под окраску 80×16 мм, полуглянцевая	Tikkurila F497 «Paper»	3,7 м
О4	потолок	окраска, Tikkurila Anti-Reflex 2, глубокоматовая, подготовка Q3	Tikkurila F497 «Paper»	14,6 м²

Примечания

1. Размеры — в мм от чистовых поверхностей стен; условные обозначения и общие указания — лист 2.
2. Картины и зеркала крепить к основанию по паспорту изделия (закладные и анкеры — в перечне скрытых работ); крест — ось центра предмета.
3. Потолок на развёртках — по нижнему уровню У1; другие уровни потолка помещения: У2 +2,600.

					Проект: Четырёхкомнатная квартира
	Лист	№ док.	Подпись	Дата	Развёртки стен В, Г. Гостиная (пом. 11)
Дизайнер	Кырпан А.С.			05.10.26	

Стадия	Лист	Листов
П	87	111

выпуск 05.10.2026 · d0efc1af8a · стр. 87 из 111




					Проект: Четырёхкомнатная квартира
	Лист	№ док.	Подпись	Дата	
Дизайнер	Кырпан А.С.			05.10.26	Визуализация: Гардеробная 1


Стадия	Лист	Листов
П	88	111

выпуск 05.10.2026 № d0efc1af8a · стр. 88 из 111

Развёртка стены А

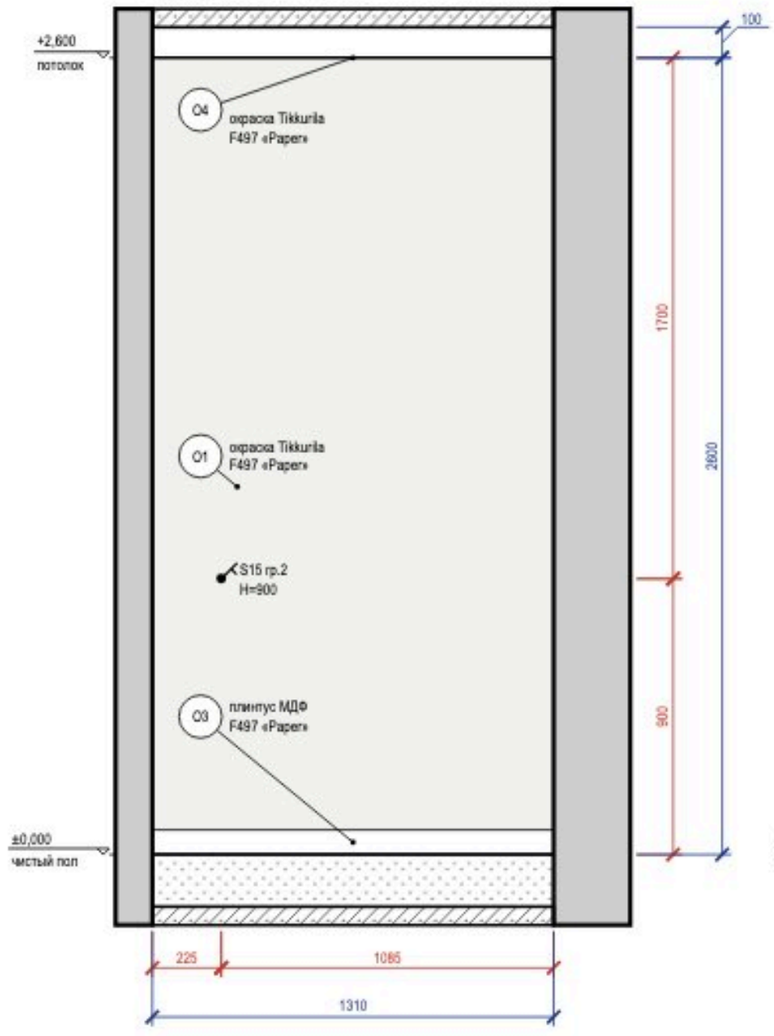

Развёртка стены Б

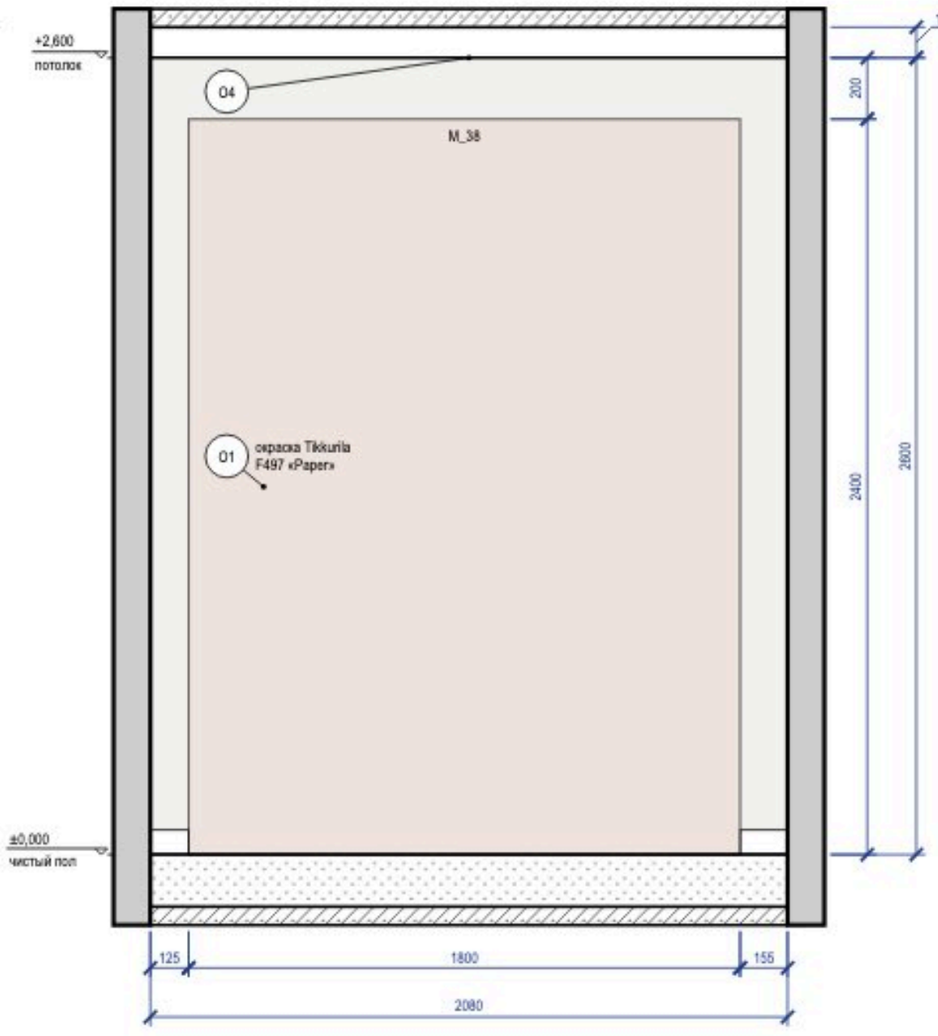

Визуализация этой стены — лист 88


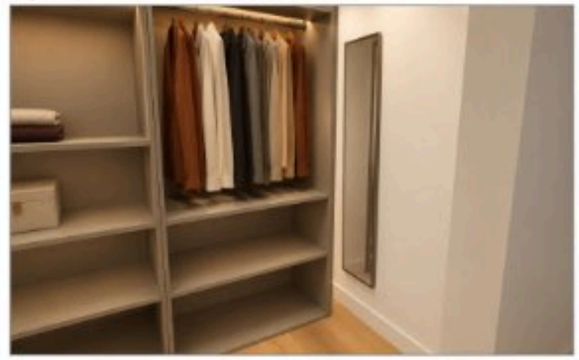


Схема развёрток (М 1:100)

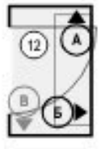

Ведомость отделки (на листе)

Марка	Поверхность	Материал, изделие	Цвет, код	Кол.
О1	стены	окраска, Tikkurila Optiva 5 Matt, матовая, подготовка К3	Tikkurila F497 «Paper»	8,8 м²
О3	плинтус	плинтус МДФ, h 80 мм, аналог: плинтус МДФ под окраску 80×16 мм, полуглянцевая	Tikkurila F497 «Paper»	1,6 м
О4	потолок	окраска, Tikkurila Anti-Reflex 2, глубокоматовая, подготовка Q3	Tikkurila F497 «Paper»	2,8 м²

Примечания

1. Размеры — в мм от чистовых поверхностей стен; условные обозначения и общие указания — лист 2.

	Лист	№ док.	Подпись	Дата	Проект: Четырёхкомнатная квартира
Дизайнер	Кырпан А.С.			05.10.26	Развёртки стен А, Б. Гардеробная 1 (пом. 12)

Стадия	Лист	Листов
П	89	111

выпуск 05.10.2026 № d0efc1af8a · стр. 89 из 111

Развёртка стены В

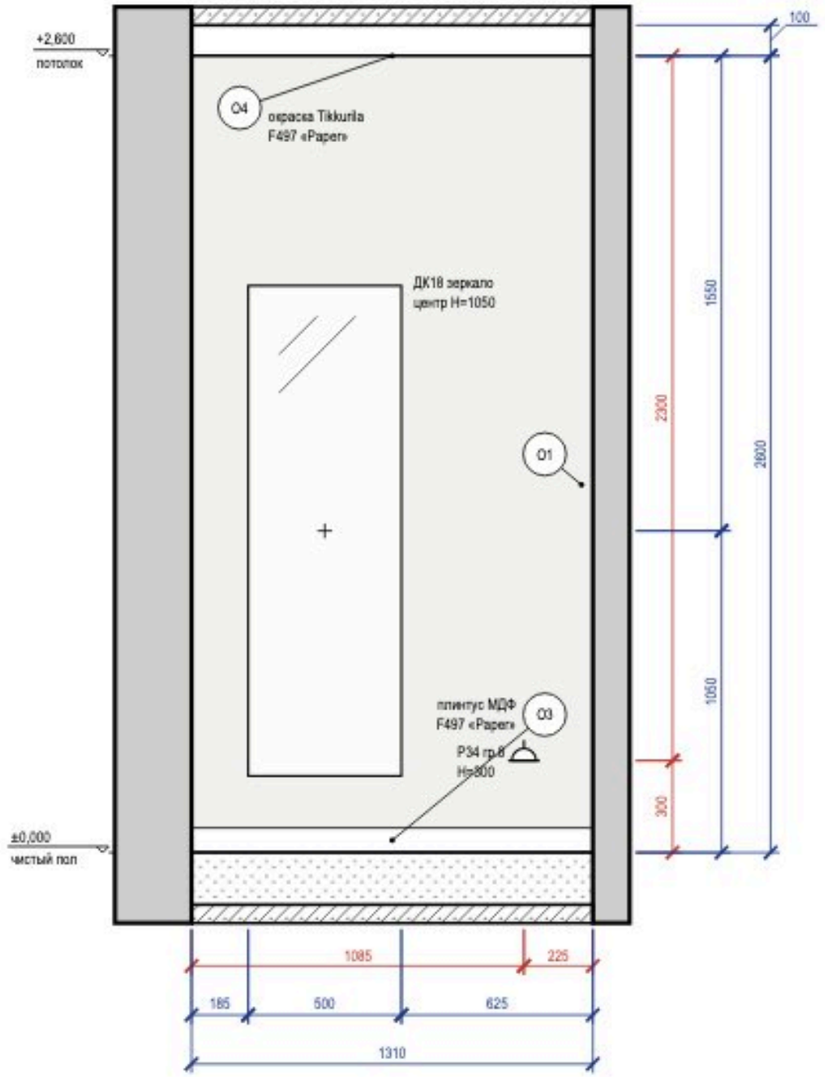


Схема развёрток (М 1:100)



Ведомость отделки (на листе)

Марка	Поверхность	Материал, изделие	Цвет, код	Кол.
О1	стены	окраска, Tikkurila Optiva 5 Matt, матовая, подготовка К3	Tikkurila F497 «Paper»	3,4 м²
О3	плинтус	плинтус МДФ, h 80 мм, аналог: плинтус МДФ под окраску 80×16 мм, полуглянцевая	Tikkurila F497 «Paper»	1,3 м
О4	потолок	окраска, Tikkurila Anti-Reflex 2, глубокоматовая, подготовка Q3	Tikkurila F497 «Paper»	2,8 м²

Примечания

1. Размеры — в мм от чистовых поверхностей стен; условные обозначения и общие указания — лист 2.
2. Картины и зеркала крепить к основанию по паспорту изделия (закладные и анкеры — в перечне скрытых работ); крест — ось центра предмета.

					Проект: Четырёхкомнатная квартира
	Лист	№ док.	Подпись	Дата	Развёртка стены В. Гардеробная 1 (пом. 12)
Дизайнер	Кырпан А.С.			05.10.26	

Стадия	Лист	Листов
П	90	111


выпуск 05.10.2026 · d0efc1af8a · стр. 90 из 111



					Проект: Четырёхкомнатная квартира	
	Лист	№ док.	Подпись	Дата		
Дизайнер	Кырпан А.С.			05.10.26	Визуализация: Балкон 1	Стадия / Лист / Листов
						П / 91 / 111

выпуск 05.10.2026 · d0efc1af8a · стр. 91 из 111

Развёртка стены А

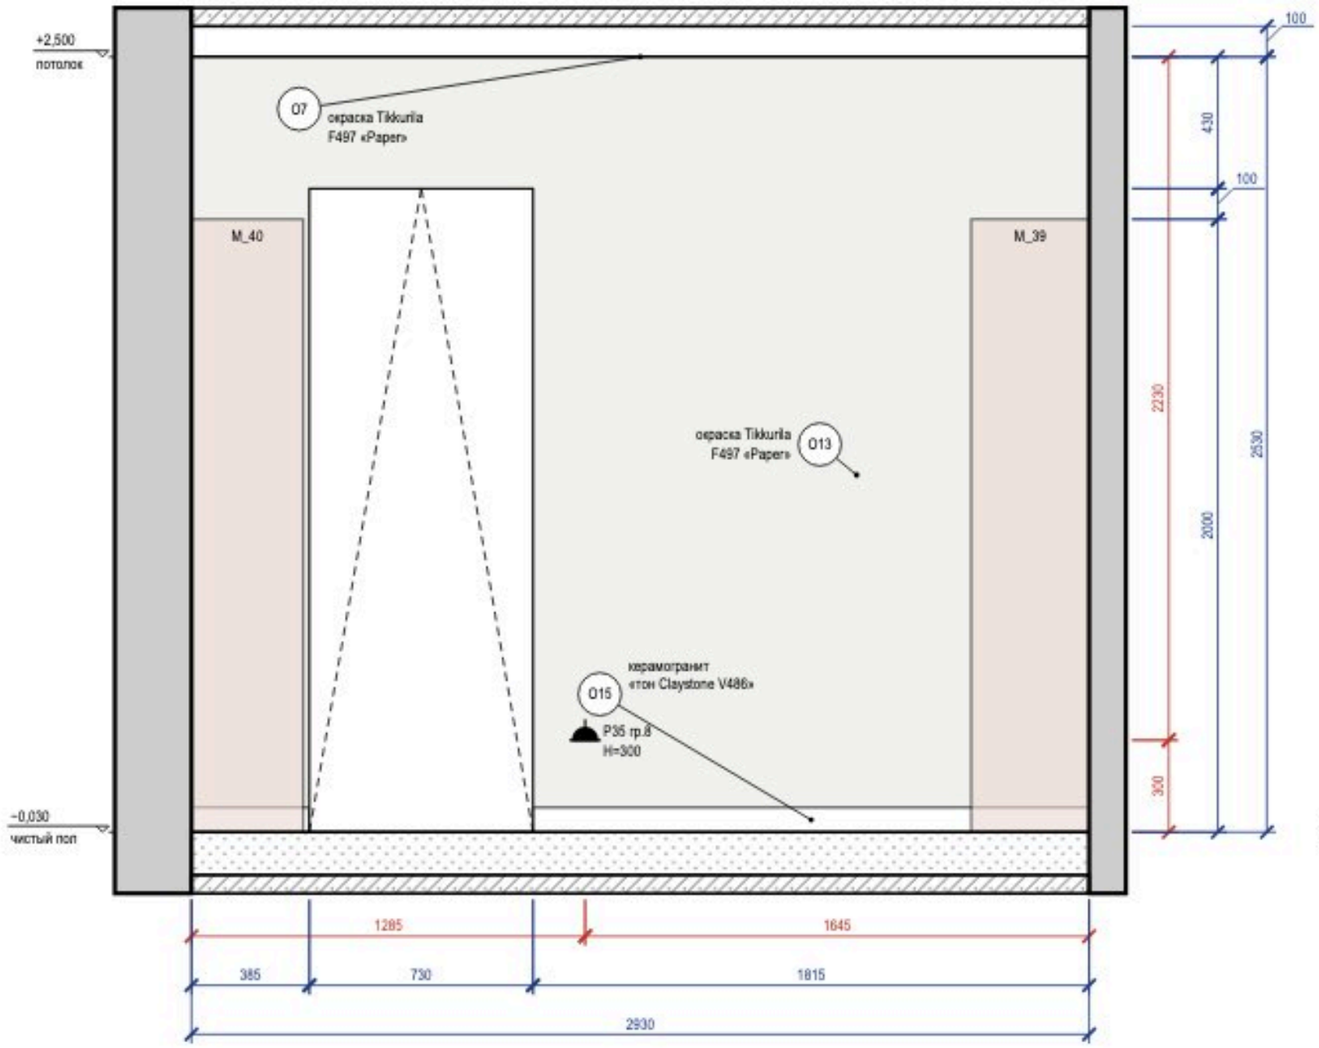

Развёртка стены Б

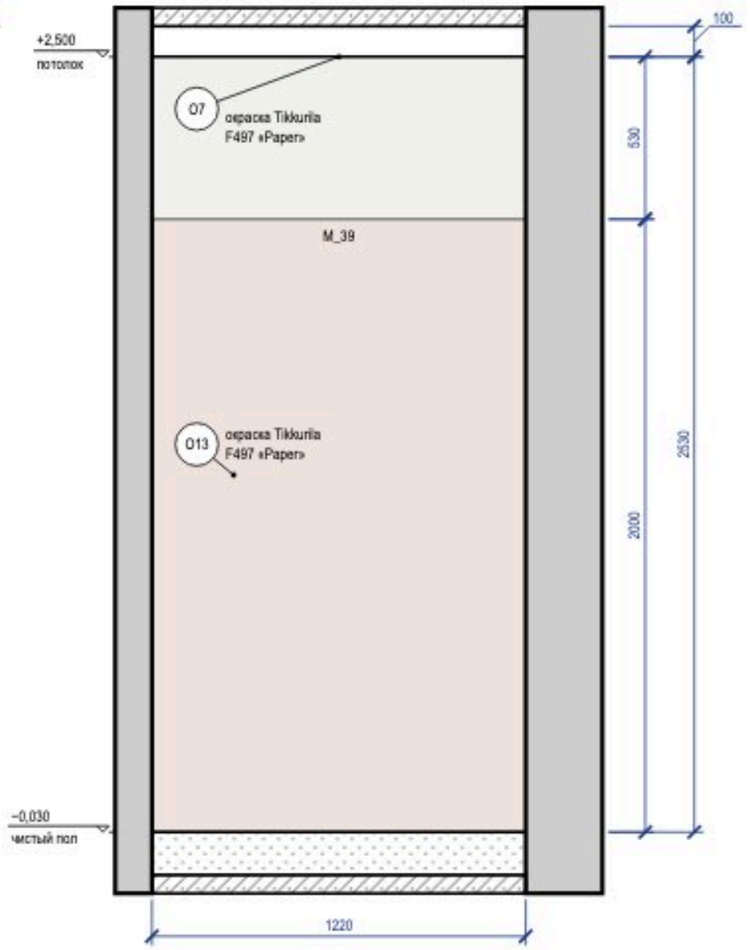


Схема развёрток (М 1:100)



Ведомость отделки (на листе)

Марка	Поверх ность	Материал, изделие	Цвет, код	Кол.
О7	потолок	окраска, Tikkurila Luja 7, матовая, подготовка Q3	Tikkurila F497 «Paper»	3,7 м²
О13	стены	окраска, Tikkurila Luja 7, шелковисто-матовая, подготовка К3	Tikkurila F497 «Paper»	9 м²
О15	плинтус	керамогранит, аналог: плинтус из керамогранита пола, подрезка 80 мм, верхняя кромка с запилом 45°	#B8AFA5 «тон Claystone V486»	2,2 м

Примечания


1. Размеры — в мм от чистовых поверхностей стен; условные обозначения и общие указания — лист 2.

					Проект: Четырёхкомнатная квартира
	Лист	№ док.	Подпись	Дата	Развёртки стен А, Б. Балкон 1 (пом. 13)
Дизайнер	Кырпан А.С.			05.10.26	

Стадия	Лист	Листов
П	92	111

выпуск 05.10.2026 № d0efc1af8a · стр. 92 из 111

Развёртка стены В

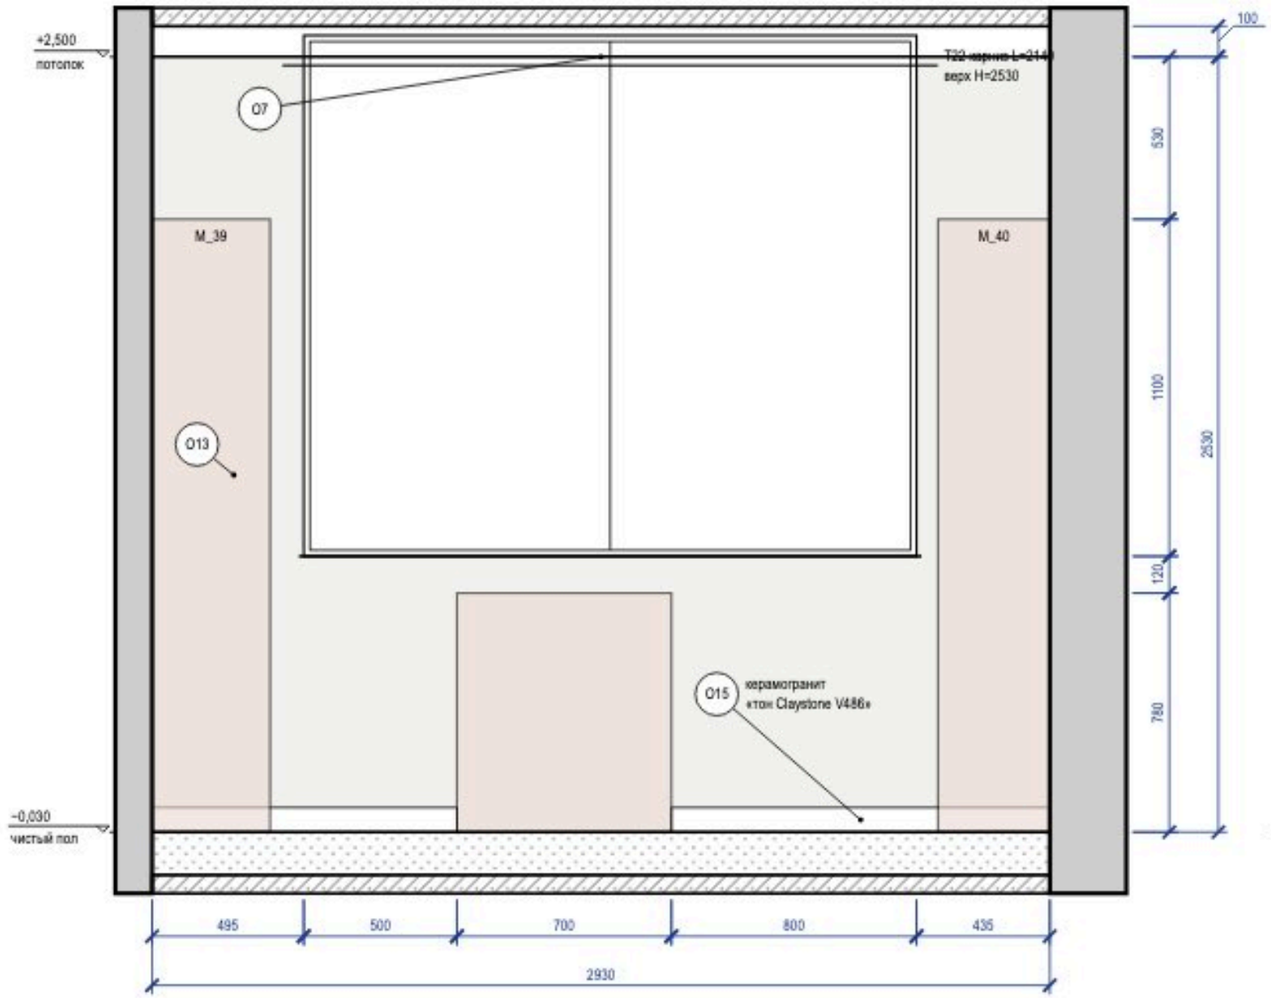

Развёртка стены Г

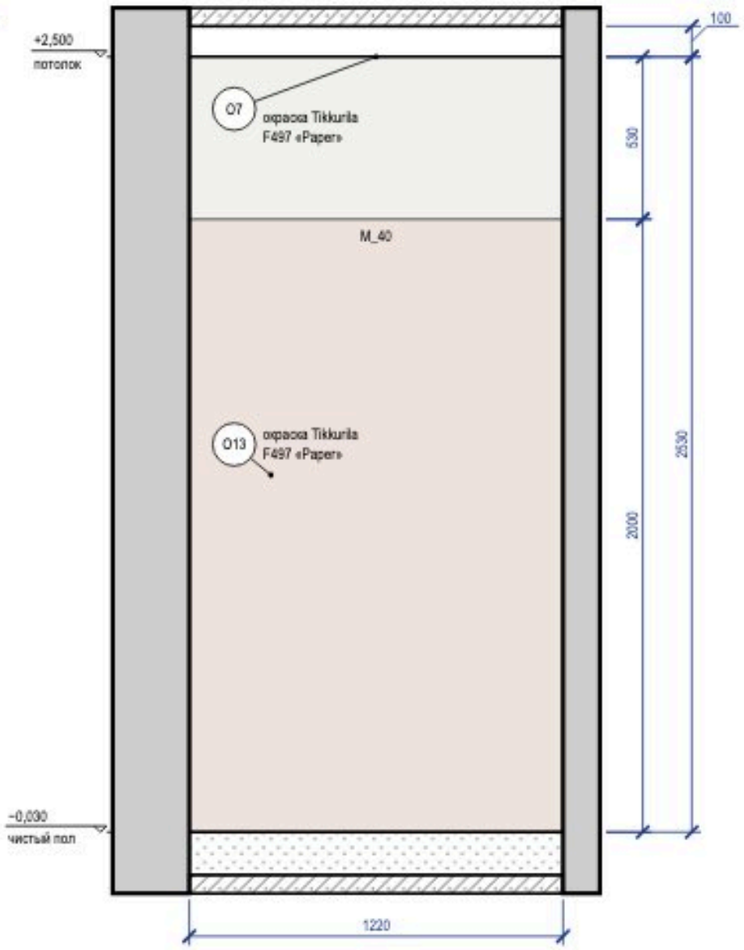



Схема развёрток (М 1:100)



Ведомость отделки (на листе)

Марка	Поверхность	Материал, изделие	Цвет, код	Кол.
О7	потолок	окраска, Tikkurila Luja 7, матовая, подготовка Q3	Tikkurila F497 «Paper»	3,7 м²
О13	стены	окраска, Tikkurila Luja 7, шелковисто-матовая, подготовка K3	Tikkurila F497 «Paper»	7,2 м²
О15	плинтус	керамогранит, аналог: плинтус из керамогранита пола, подрезка 80 мм, верхняя кромка с запилом 45°	#B8AFA5 «тон Claystone V486»	2,2 м

Визуализация этой стены — лист 91

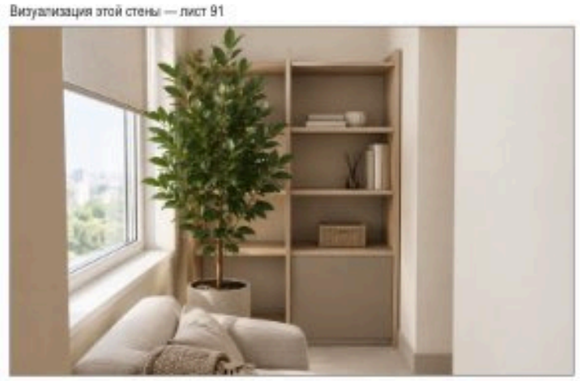

Примечания


1. Размеры — в мм от чистовых поверхностей стен; условные обозначения и общие указания — лист 2.
2. Карнизы (шины) — по ведомости текстиля декоратора; длина L и верх H — по развёртке, крепление — до окраски потолка.

					Проект: Четырёхкомнатная квартира
	Лист	№ док.	Подпись	Дата	Развёртки стен В, Г. Балкон 1 (пом. 13)
Дизайнер	Кырпан А.С.			05.10.26	


Стадия	Лист	Листов
П	93	111

выпуск 05.10.2026 № d0efc1af8a · стр. 93 из 111


Общий вид

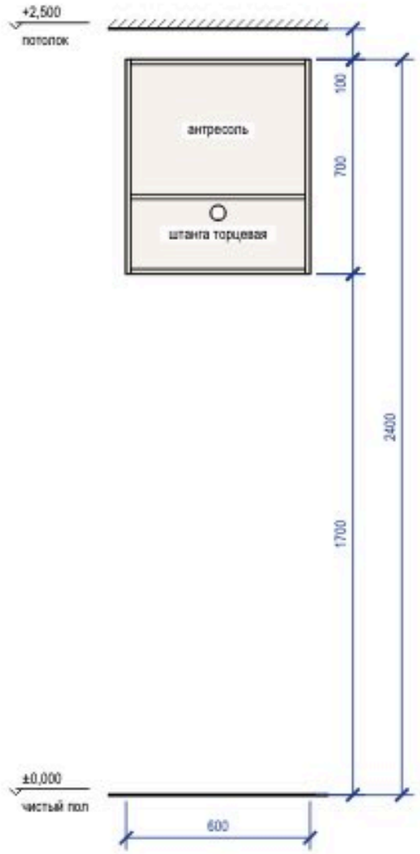

Наполнение, размеры в свету

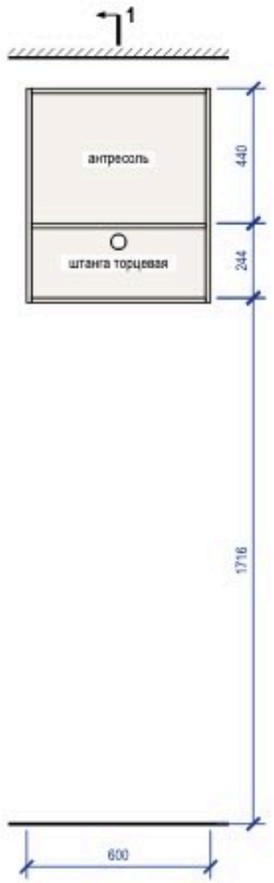


Разрез 1-1

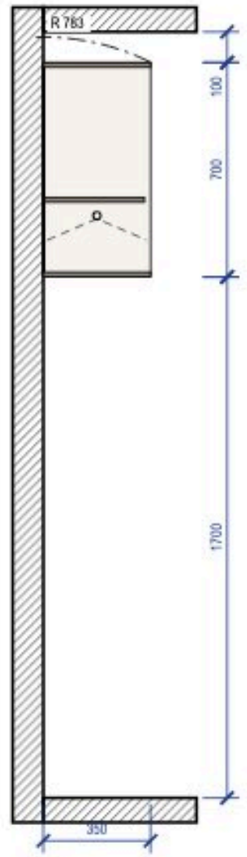

Примечания

1. Размеры — в мм по чистовой отделке; изделие 600×350×700 (Ш×Г×В). Перед раскроем — контрольный замер цеха после чистовой отделки стен, пола и потолка.
2. Корпус — ЛДСП 16 мм, задняя стенка ХДФ 4 мм в паз, цоколь 0 мм на регулируемых опорах; открытая система без фасадов, ящики с фасадами.
3. Кромка: скрытые торцы 0,4 мм, видимые 2 мм (ПВХ/АБС).
4. Номинальные зазоры: между фасадами ящиков 3 мм, фасад ящика — стойка 2 мм.
5. Ящики — направляющие полного выдвижения NL 300 (внутренняя глубина 346 мм ≥ NL + 3); присадка по 32-й системе — выполняет цех.
6. Зазор до потолка 100 мм — закрыть планкой в цвет корпуса при монтаже.
7. Подъём корпуса: диагональ боковины $\sqrt{(700^2 + 350^2)} = 783$ мм < 800 мм до потолка — корпус собирается лёжа и поднимается поворотом.
8. Крепление к стене от опрокидывания: крепление к стене, 2 точки; основание стены и шаг анкеров — монтажная схема шкафов.


3D орто

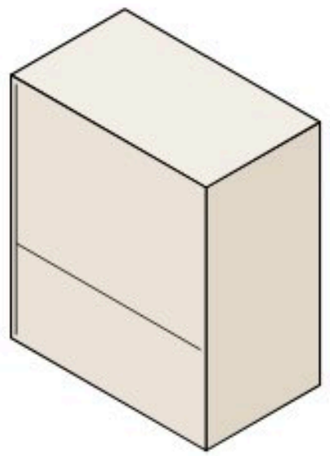


					Проект: Четырёхкомнатная квартира			
	Лист	№ док.	Подпись	Дата	Система хранения M_07	Стадия	Лист	Листов
Дизайнер	Кырпан А.С.			05.10.26		П	Д_1	111

выпуск 05.10.2026 · d0efc1af8a · стр. 94 из 111


Общий вид

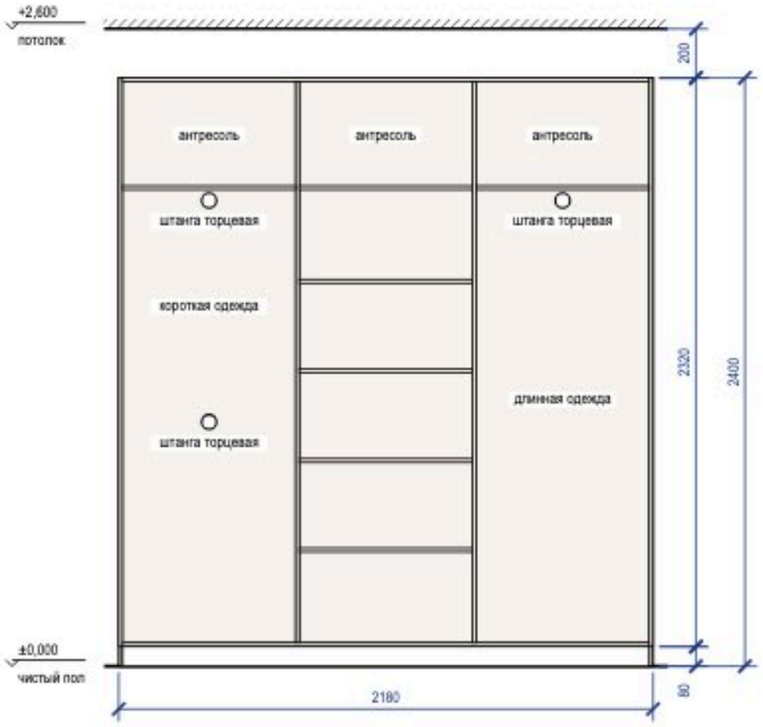


Наполнение, размеры в свету

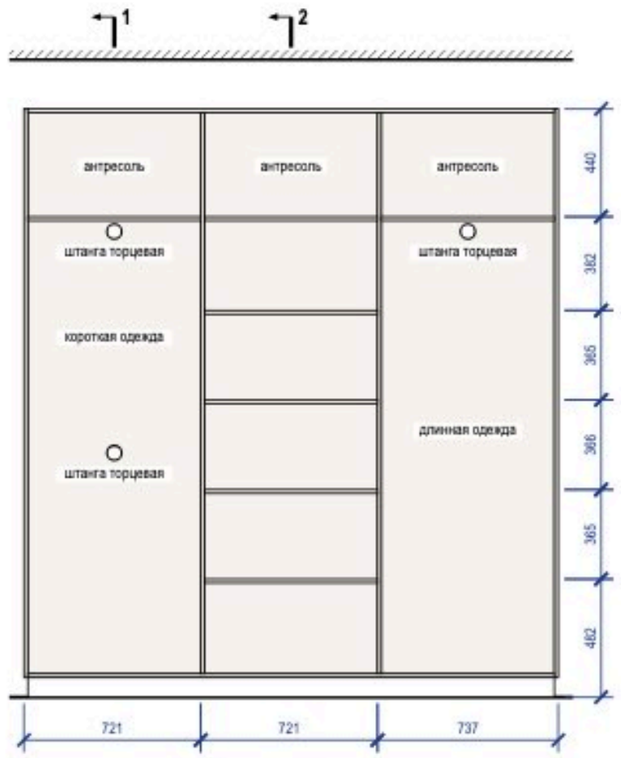

Разрез 1-1

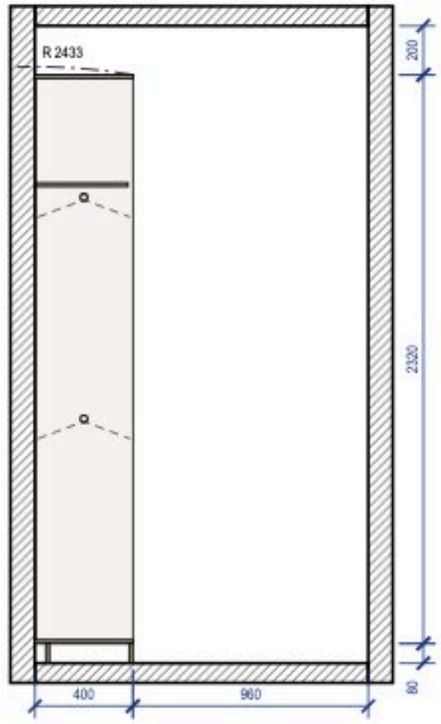


Разрез 2-2

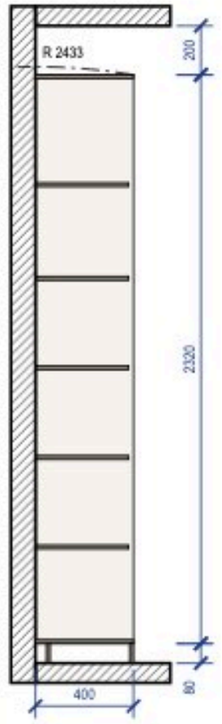

Примечания

1. Размеры — в мм по чистовой отделке; изделие 2180×400×2400 (Ш×Г×В). Перед раскроем — контрольный замер цеха после чистовой отделки стен, пола и потолка.
2. Корпус — ЛДСП 16 мм, задняя стенка ХДФ 4 мм в паз, цоколь 80 мм на регулируемых опорах; открытая система без фасадов, ящики с фасадами.
3. Кромка: скрытые торцы 0,4 мм, видимые 2 мм (ПВХ/АБС).
4. Номинальные зазоры: между фасадами ящиков 3 мм, фасад ящика — стойка 2 мм.
5. Ящики — направляющие полного выдвижения NL 350 (внутренняя глубина 396 мм ≥ NL + 3); присадка по 32-й системе — выполняет цех.
6. Зазор до потолка 200 мм.
7. Подъём корпуса: диагональ боковины $\sqrt{(2400^2 + 400^2)} = 2433$ мм < 2600 мм до потолка — корпус собирается лёжа и поднимается поворотом.
8. Крепление к стене от опрокидывания: крепление к стене, 4 точки; основание стены и шаг анкеров — монтажная схема шкафов.
9. Проход перед изделием 960 мм показан на разрезе 1-1.


3D орто

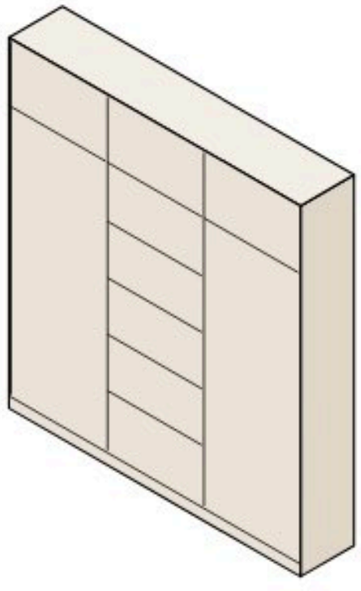


					Проект: Четырёхкомнатная квартира			
	Лист	№ док.	Подпись	Дата	Система хранения М_08	Стадия	Лист	Листов
Дизайнер	Кырпан А.С.			05.10.26		П	Д_2	111

выпуск 05.10.2026 · d0efc1af8a · стр. 95 из 111


Общий вид

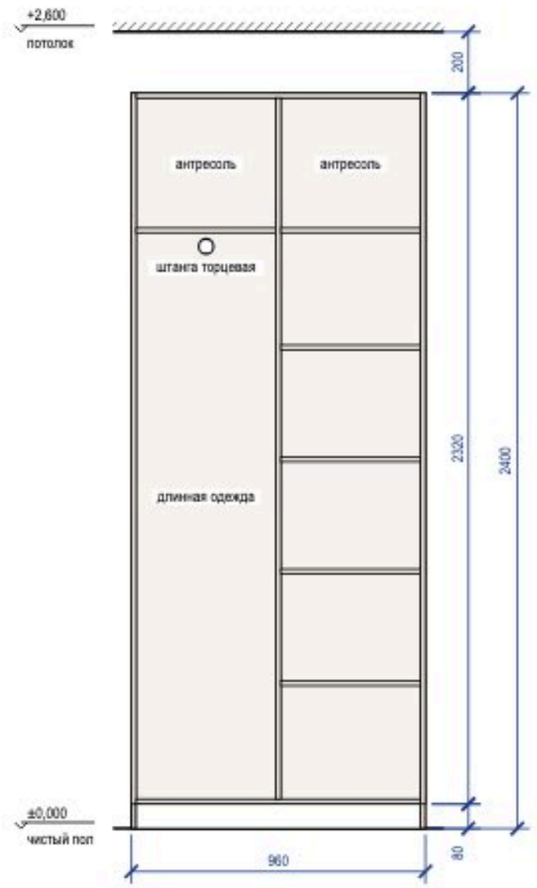


Наполнение, размеры в свету

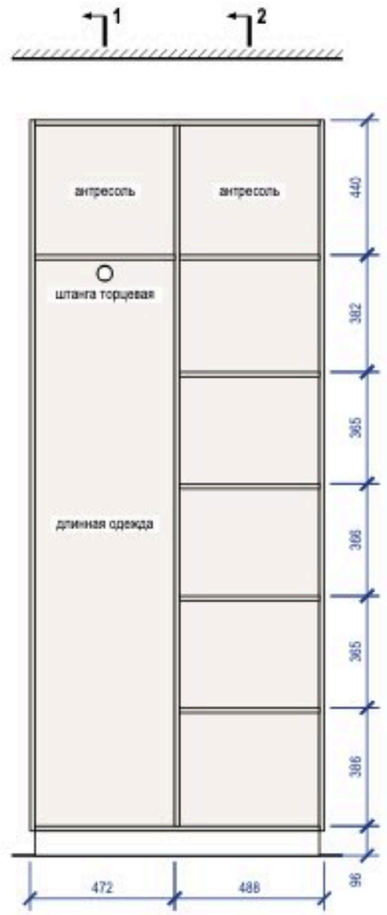

Разрез 1-1

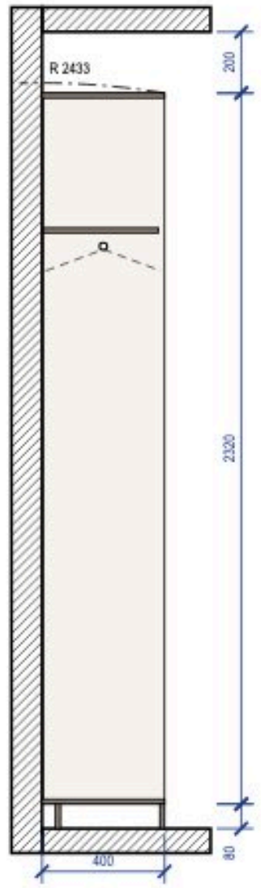


Разрез 2-2

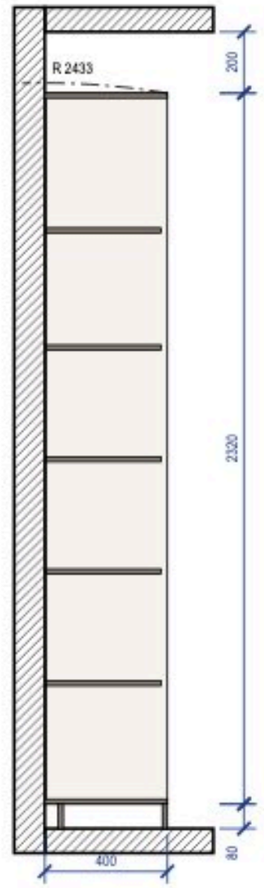

Примечания

1. Размеры — в мм по чистовой отделке; изделие 960×400×2400 (Ш×Г×В). Перед раскроем — контрольный замер цеха после чистовой отделки стен, пола и потолка.
2. Корпус — ЛДСП 16 мм, задняя стенка ХДФ 4 мм в паз, цоколь 80 мм на регулируемых опорах; открытая система без фасадов, ящики с фасадами.
3. Кромка: скрытые торцы 0,4 мм, видимые 2 мм (ПВХ/АБС).
4. Номинальные зазоры: между фасадами ящиков 3 мм, фасад ящика — стойка 2 мм.
5. Ящики — направляющие полного выдвижения NL 350 (внутренняя глубина 396 мм ≥ NL + 3); присадка по 32-й системе — выполняет цех.
6. Зазор до потолка 200 мм.
7. Подъём корпуса: диагональ боковины $\sqrt{(2400^2 + 400^2)} = 2433$ мм < 2600 мм до потолка — корпус собирается лёжа и поднимается поворотом.
8. Крепление к стене от опрокидывания: крепление к стене, 3 точки; основание стены и шаг анкеров — монтажная схема шкафов.


3D орто

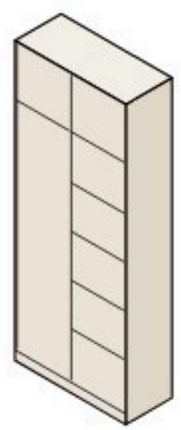


					Проект: Четырёхкомнатная квартира		
	Лист	№ док.	Подпись	Дата			
Дизайнер	Кырпан А.С.			05.10.26	Система хранения M_09	Стадия	Лист	Листов
						П	Д_3	111

выпуск 05.10.2026 · d0efc1af8a · стр. 96 из 111


Вид с фасадами

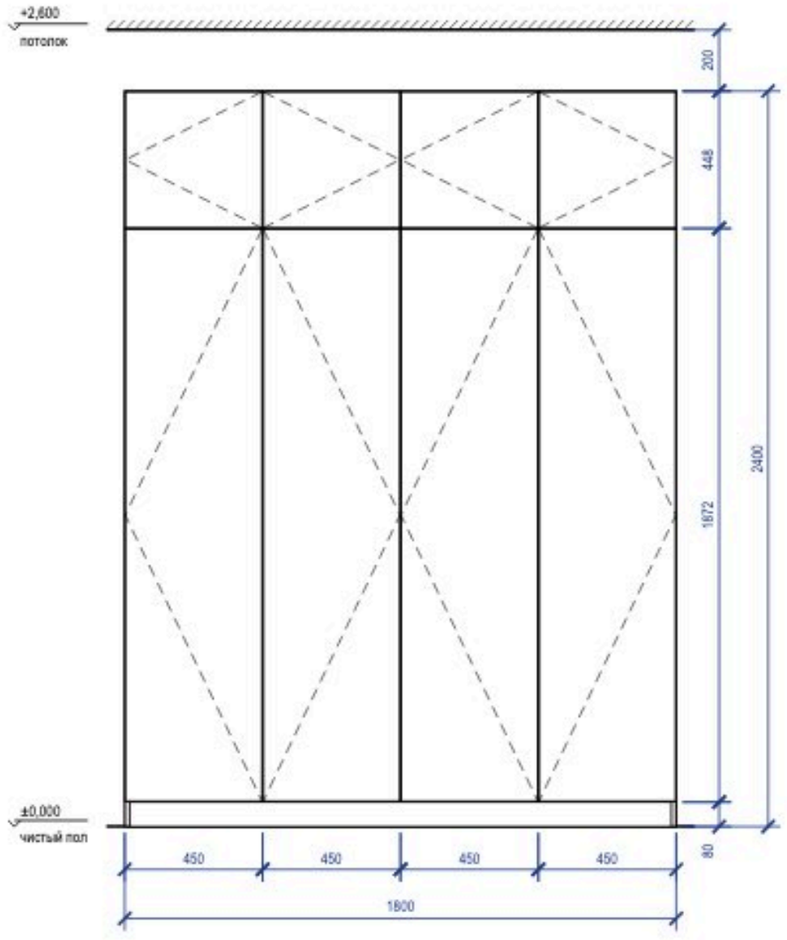


Вид без фасадов

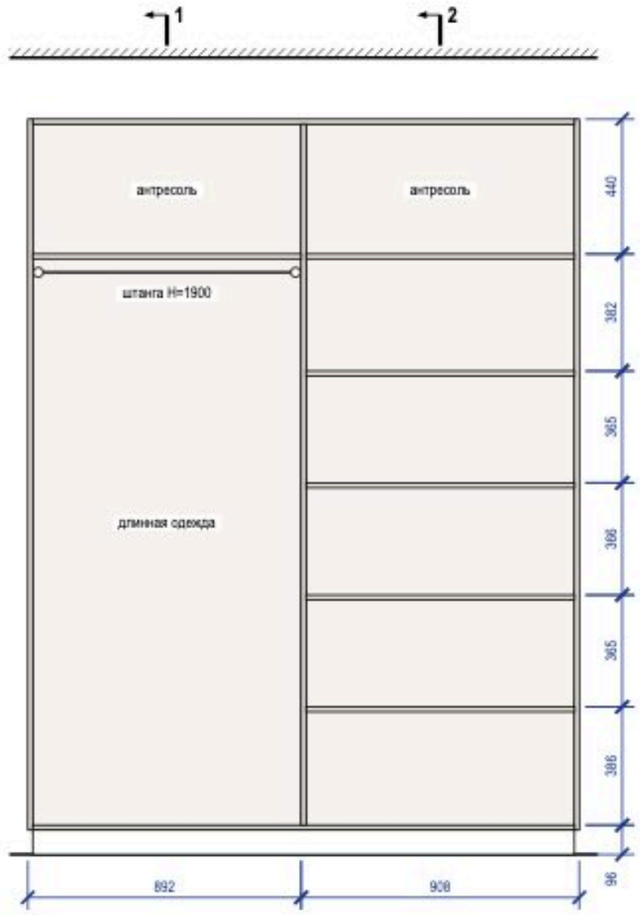

Разрез 1-1

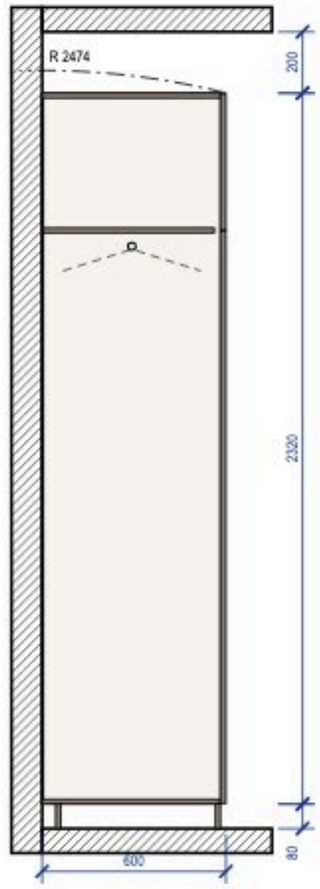


Разрез 2-2

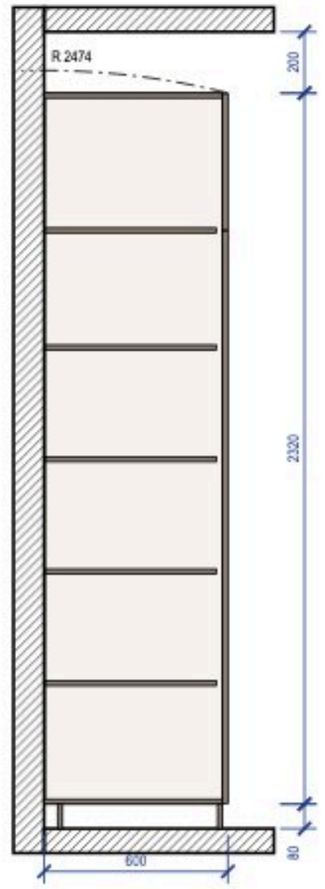

Примечания

1. Размеры — в мм по чистовой отделке; изделие 1800×600×2400 (Ш×Г×В). Перед раскроем — контрольный замер цеха после чистовой отделки стен, пола и потолка.
2. Корпус — ЛДСП 16 мм, задняя стенка ХДФ 4 мм в паз, цоколь 80 мм на регулируемых опорах; фасады — МДФ, эмаль матовая 18 мм накладные, цвет — по колерной карте; петли с доводчиком: фасад 1869 мм — 4 петли, фасад 445 мм — 2 петли.
3. Кромка: скрытые торцы 0,4 мм, видимые 2 мм (ПВХ/АБС).
4. Номинальные зазоры: между фасадами 3 мм, фасад — стена и фасад — потолок не менее 3 мм, фасад ящика — стойка 2 мм.
5. Ящики — направляющие полного выдвижения NL 550 (внутренняя глубина 578 мм ≥ NL + 3); присадка по 32-й системе — выполняет цех.
6. Зазор до потолка 200 мм.
7. Подъём корпуса: диагональ боковины $\sqrt{(2400^2 + 600^2)} = 2474$ мм < 2600 мм до потолка — корпус собирается лёжа и поднимается поворотом.
8. Крепление к стене от опрокидывания: уголок к стене, 3 шт.; основание стены и шаг анкеров — монтажная схема шкафов.


3D орто

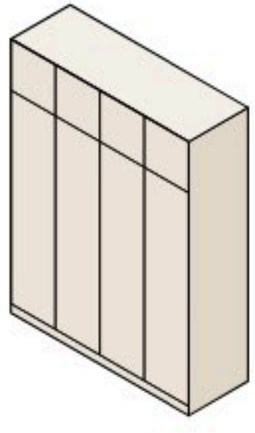


					Проект: Четырёхкомнатная квартира		
	Лист	№ док.	Подпись	Дата	Шкаф распашной М_15	Стадия	Лист	Листов
Дизайнер	Кырпан А.С.			05.10.26		П	Д_4	111

выпуск 05.10.2026 · d0efc1af8a · стр. 97 из 111


Общий вид

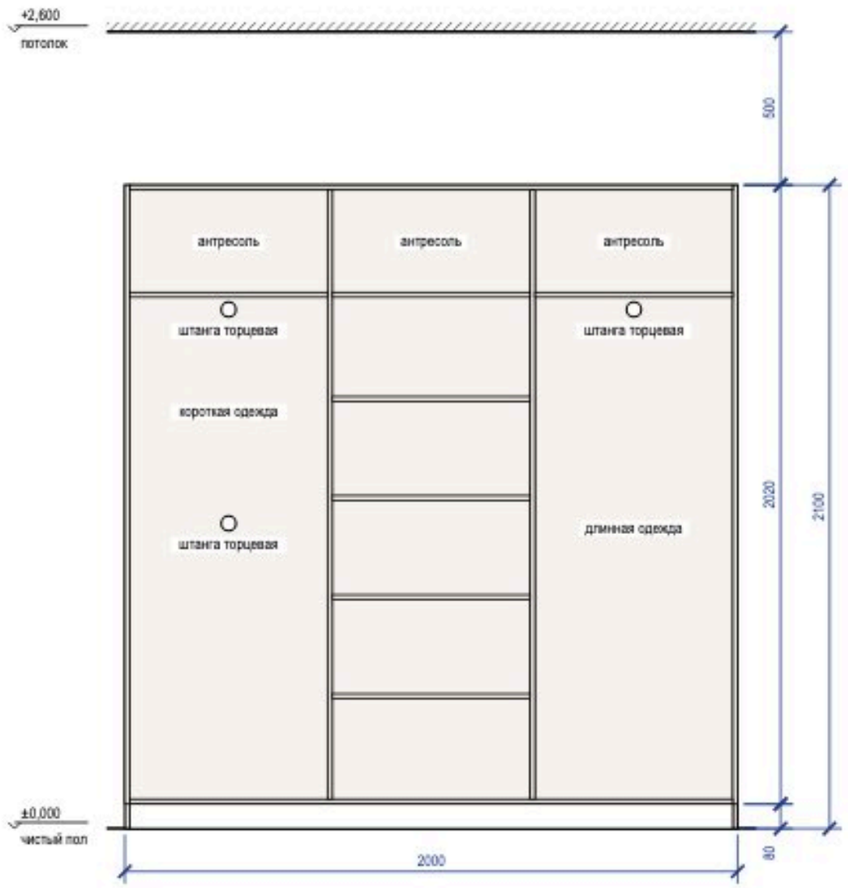


Наполнение, размеры в свету

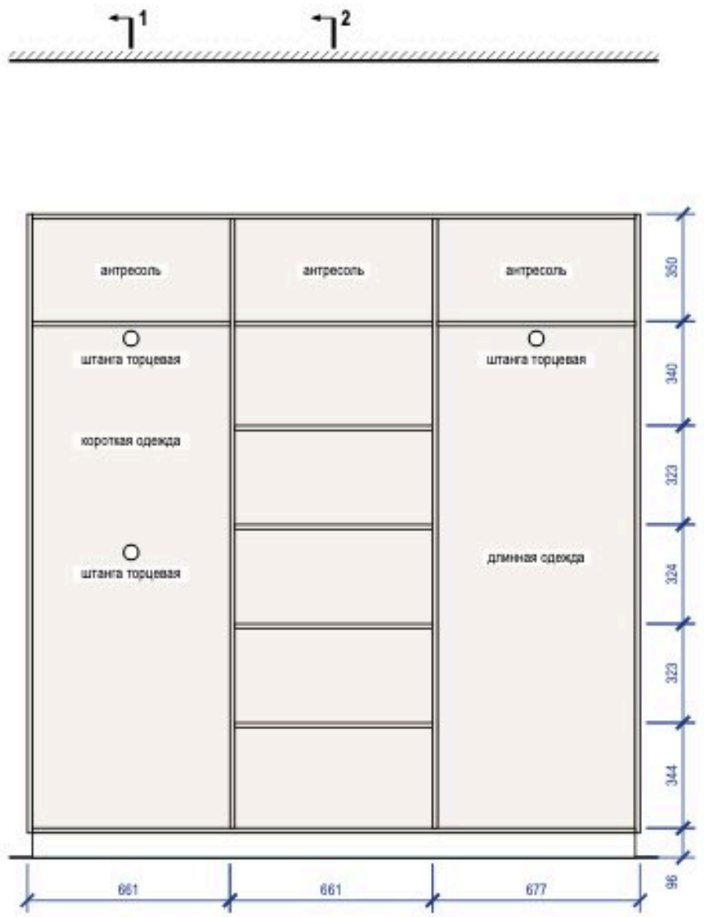

Разрез 1-1

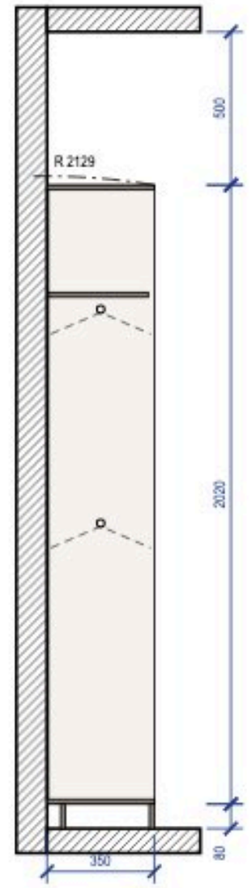


Разрез 2-2

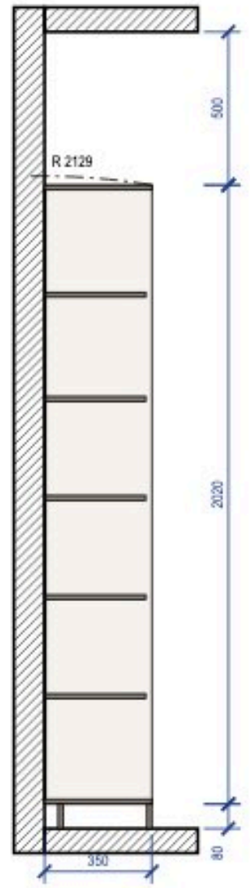

Примечания

1. Размеры — в мм по чистовой отделке; изделие 2000×350×2100 (Ш×Г×В). Перед раскроем — контрольный замер цеха после чистовой отделки стен, пола и потолка.
2. Корпус — ЛДСП 16 мм, задняя стенка ХДФ 4 мм в паз, цоколь 80 мм на регулируемых опорах; открытая система без фасадов, ящики с фасадами.
3. Кромка: скрытые торцы 0,4 мм, видимые 2 мм (ПВХ/АБС).
4. Номинальные зазоры: между фасадами ящиков 3 мм, фасад ящика — стойка 2 мм.
5. Ящики — направляющие полного выдвижения NL 300 (внутренняя глубина 346 мм ≥ NL + 3); присадка по 32-й системе — выполняет цех.
6. Зазор до потолка 500 мм.
7. Подъём корпуса: диагональ боковины $\sqrt{(2100^2 + 350^2)} = 2129$ мм < 2600 мм до потолка — корпус собирается лёжа и поднимается поворотом.
8. Крепление к стене от опрокидывания: крепление к стене, 3 точки; основание стены и шаг анкеров — монтажная схема шкафов.


3D орто

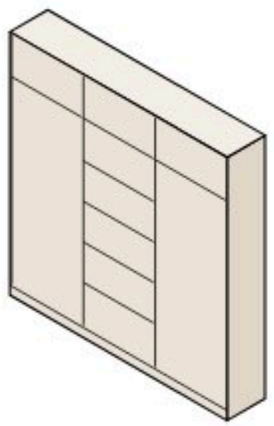

					Проект: Четырёхкомнатная квартира			
	Лист	№ док.	Подпись	Дата	Система хранения M_17	Стадия	Лист	Листов
Дизайнер	Кырпан А.С.			05.10.26		П	Д_5	111

выпуск 05.10.2026 № d0efc1af8a · стр. 98 из 111


Вид с фасадами

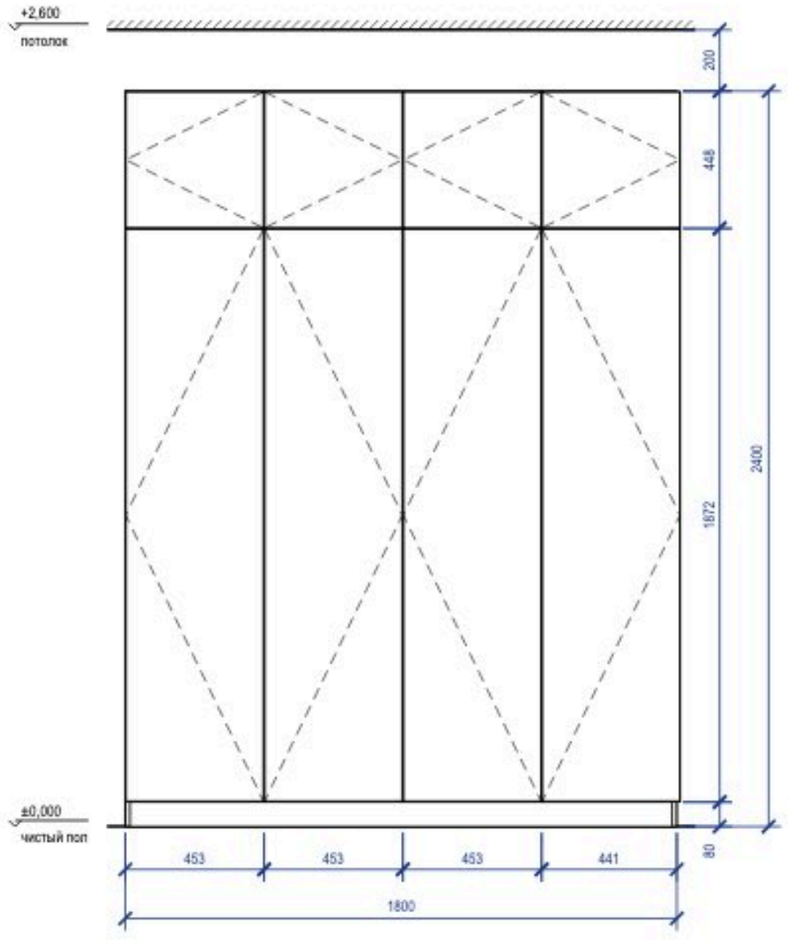

Вид без фасадов




Разрез 1-1

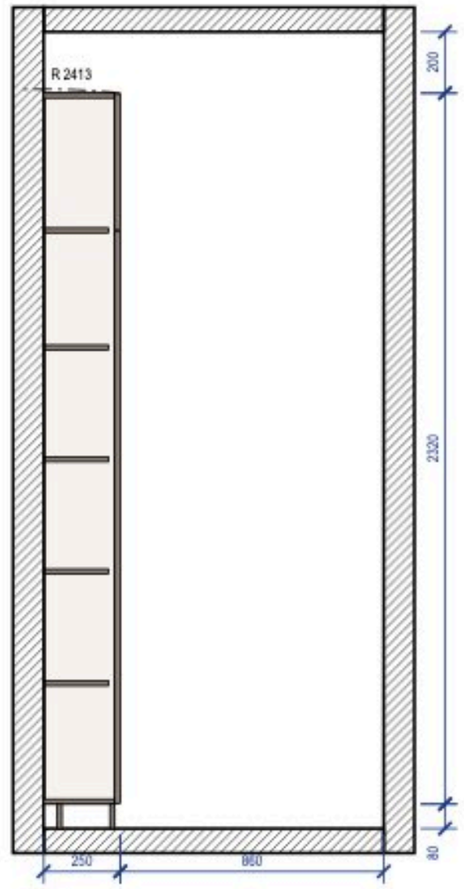

Примечания

1. Размеры — в мм по чистовой отделке; изделие 1800×250×2400 (Ш×Г×В). Перед раскроем — контрольный замер цеха после чистовой отделки стен, пола и потолка.
2. Корпус — ЛДСП 16 мм, задняя стенка ХДФ 4 мм в паз, цоколь 80 мм на регулируемых опорах; фасады — МДФ, эмаль матовая 18 мм накладные, цвет — по колерной карте; петли с доводчиком: фасад 1969 мм — 4 петли, фасад 445 мм — 2 петли.
3. Кромка: скрытые торцы 0,4 мм, видимые 2 мм (ПВХ/АБС).
4. Номинальные зазоры: между фасадами 3 мм, фасад — стена и фасад — потолок не менее 3 мм, фасад ящика — стойка 2 мм.
5. Присадка по 32-й системе — выполняет цех.
6. Зазор до потолка 200 мм.
7. Подъём корпуса: диагональ боковины $\sqrt{(2400^2 + 250^2)} = 2413$ мм < 2600 мм до потолка — корпус собирается лёжа и поднимается поворотом.
8. Крепление к стене от опрокидывания: крепление к стене, 4 точки; основание стены и шаг анкеров — монтажная схема шкафов.
9. Проход перед изделием 860 мм показан на разрезе 1-1.


3D орто

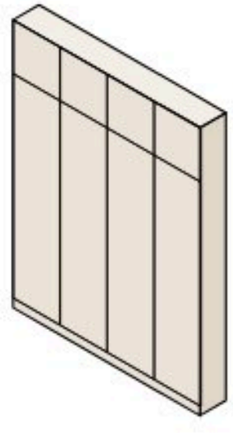


					Проект: Четырёхкомнатная квартира		
	Лист	№ док.	Подпись	Дата	Система хранения М_18	Стадия	Лист	Листов
Дизайнер	Кырпан А.С.			05.10.26		П	Д_6	111

выпуск 05.10.2026 · d0efc1af8a · стр. 99 из 111


Вид с фасадами

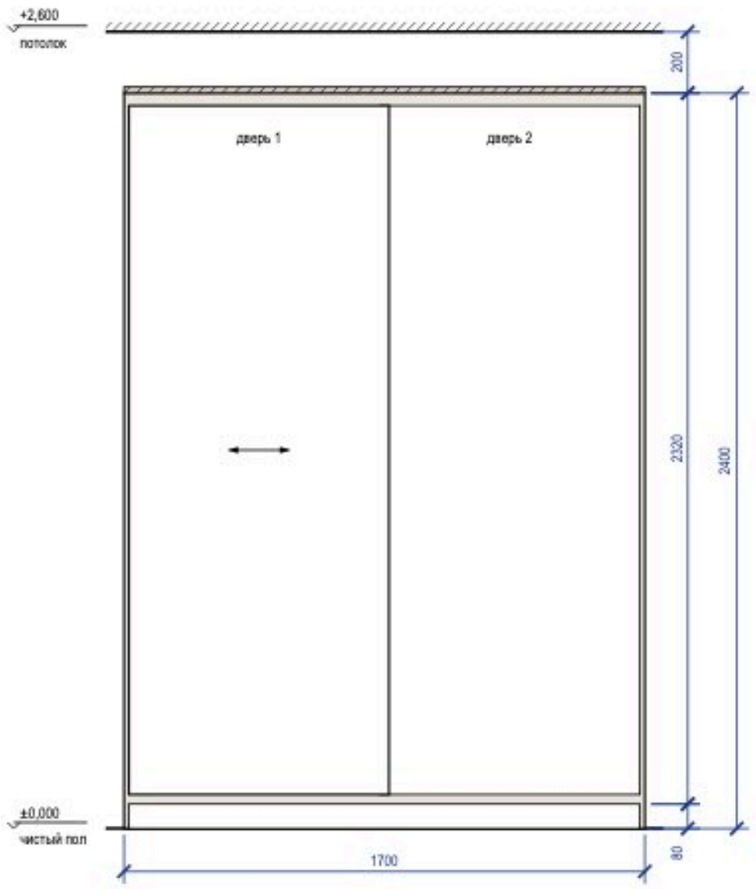


Вид без фасадов

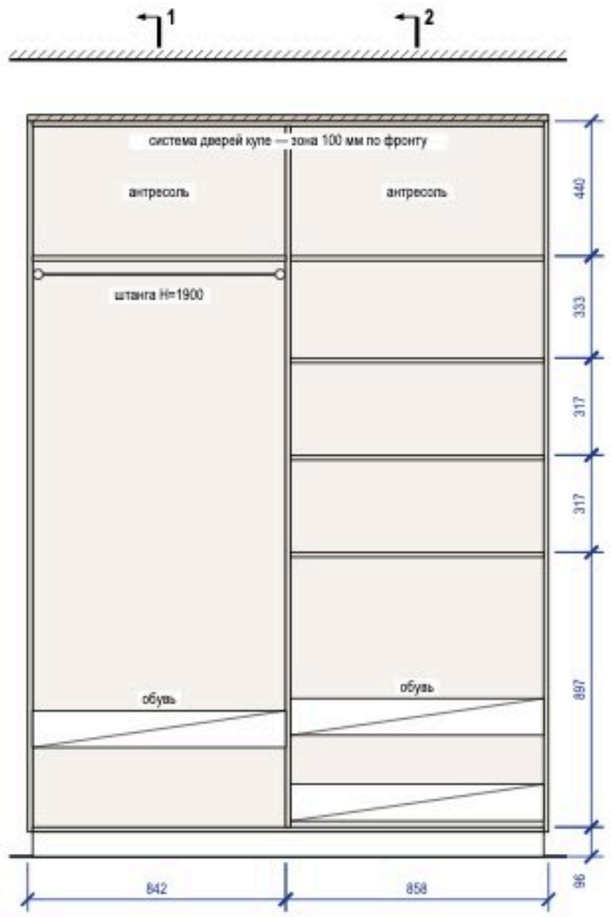

Разрез 1-1

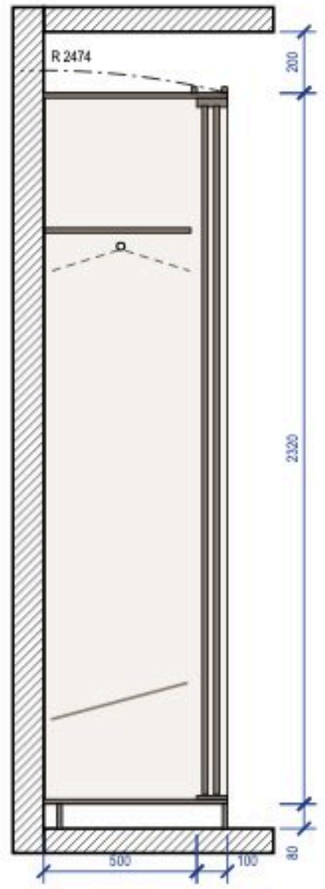


Разрез 2-2

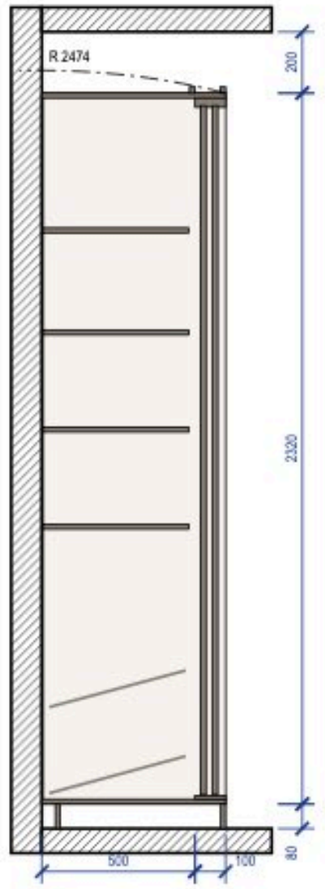

Примечания

1. Размеры — в мм по чистовой отделке; изделие 1700×600×2400 (Ш×Г×В). Перед раскроем — контрольный замер цеха после чистовой отделки стен, пола и потолка.
2. Корпус — ЛДСП 16 мм, задняя стенка ХДФ 4 мм в паз, цоколь 80 мм на регулируемых опорах; двери купе — ЛДСП 10 мм в алюминиевом профиле, нахлёст 30 мм, ширина двери 849 мм, высота — проём минус 40 мм; цвет — по колерной карте.
3. Кромка: скрытые торцы 0,4 мм, видимые 2 мм (ПВХ/АБС).
4. Номинальные зазоры: дверь купе — боковина 3 мм, фасад ящика — стойка 2 мм; ящики внутри купе — с накладкой 30 мм на стойке со стороны нахлёста дверей.
5. Ящики — направляющие полного выдвижения NL 450 (внутренняя глубина 496 мм ≥ NL + 3); присадка по 32-й системе — выполняет цех.
6. Компенсатор 20 мм — короб из ЛДСП по фронту и торцам, подгоняется к потолку при монтаже (припуск 20 мм), крепится к корпусу и к потолку.
7. Подъём корпуса: диагональ боковины $\sqrt{(2400^2 + 600^2)} = 2474$ мм < 2600 мм до потолка — корпус собирается лёжа и поднимается поворотом.
8. Крепление к стене от опрокидывания: крепление к стене, 3 точки; основание стены и шаг анкеров — монтажная схема шкафов.


3D орто

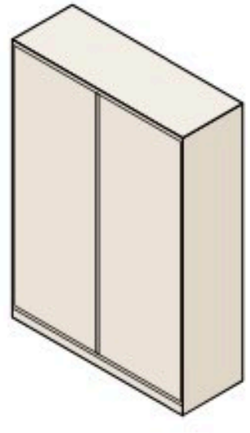


					Проект: Четырёхкомнатная квартира			
	Лист	№ док.	Подпись	Дата	Шкаф-купе M_28	Стадия	Лист	Листов
Дизайнер	Кырпан А.С.			05.10.26		П	Д_7	111

выпуск 05.10.2026 · d0efc1af8a · стр. 100 из 111


Общий вид

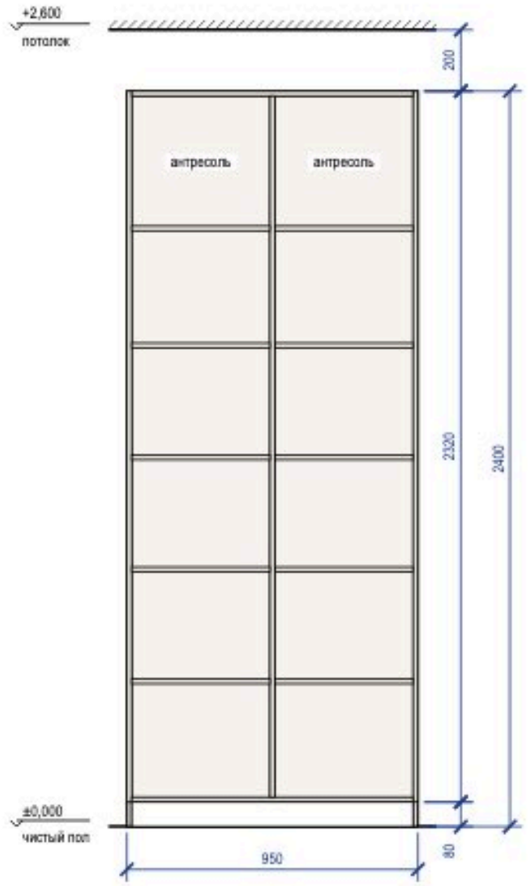

Наполнение, размеры в свету

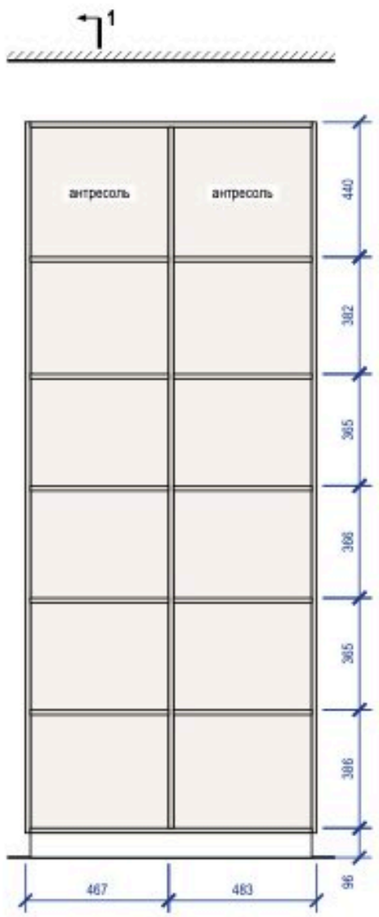


Разрез 1-1

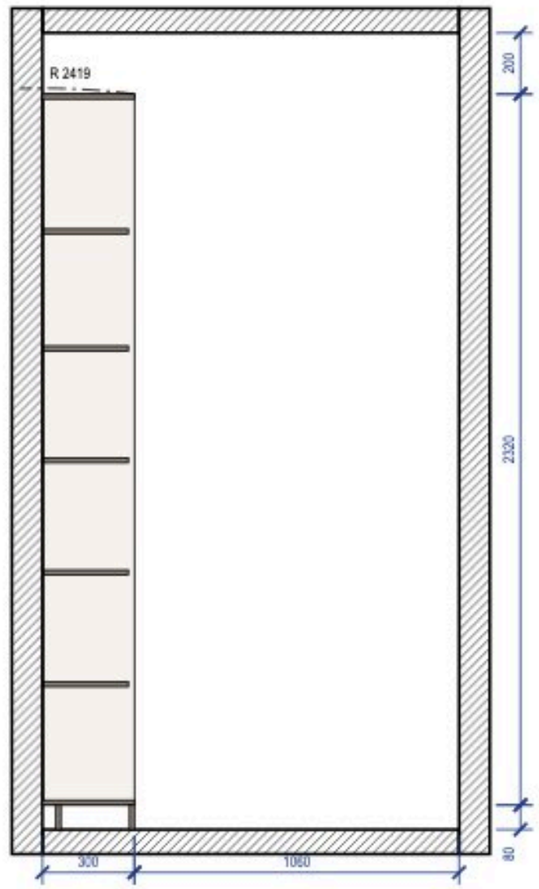

Примечания

1. Размеры — в мм по чистовой отделке; изделие 950×300×2400 (Ш×Г×В). Перед раскроем — контрольный замер цеха после чистовой отделки стен, пола и потолка.
2. Корпус — ЛДСП 16 мм, задняя стенка ХДФ 4 мм в паз, цоколь 80 мм на регулируемых опорах; открытая система без фасадов, ящики с фасадами.
3. Кромка: скрытые торцы 0,4 мм, видимые 2 мм (ПВХ/АБС).
4. Номинальные зазоры: между фасадами ящиков 3 мм, фасад ящика — стойка 2 мм.
5. Ящики — направляющие полного выдвижения NL 270 (внутренняя глубина 296 мм ≥ NL + 3); присадка по 32-й системе — выполняет цех.
6. Зазор до потолка 200 мм.
7. Подъём корпуса: диагональ боковины $\sqrt{(2400^2 + 300^2)} = 2419$ мм < 2600 мм до потолка — корпус собирается лёжа и поднимается поворотом.
8. Крепление к стене от опрокидывания: крепление к стене, 3 точки; основание стены и шаг анкеров — монтажная схема шкафов.
9. Проход перед изделием 1060 мм показан на разрезе 1-1.


3D орто

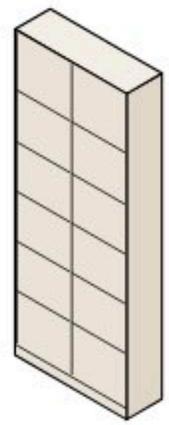


					Проект: Четырёхкомнатная квартира		
	Лист	№ док.	Подпись	Дата			
Дизайнер	Кырпан А.С.			05.10.26	Система хранения M_31	Стадия	Лист	Листов
						П	Д_8	111

выпуск 05.10.2026 · d0efc1af8a · стр. 101 из 111


Общий вид

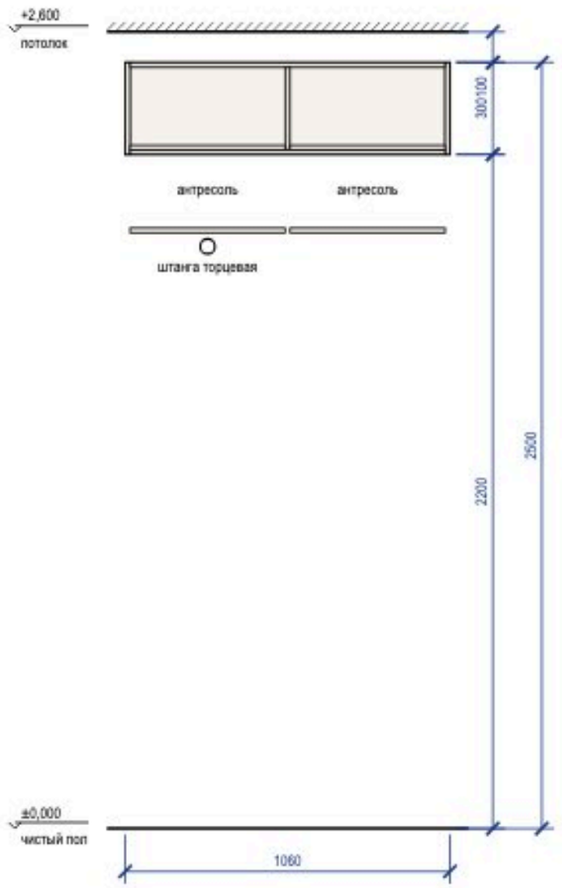


Наполнение, размеры в свету

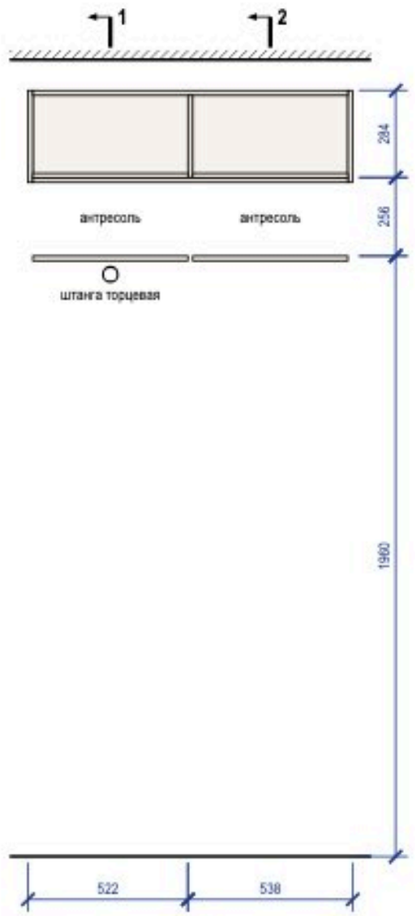

Разрез 1-1

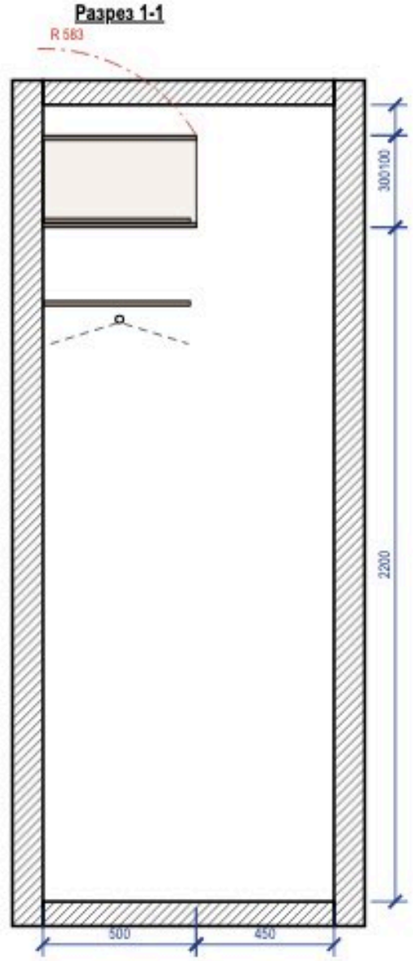


Разрез 2-2

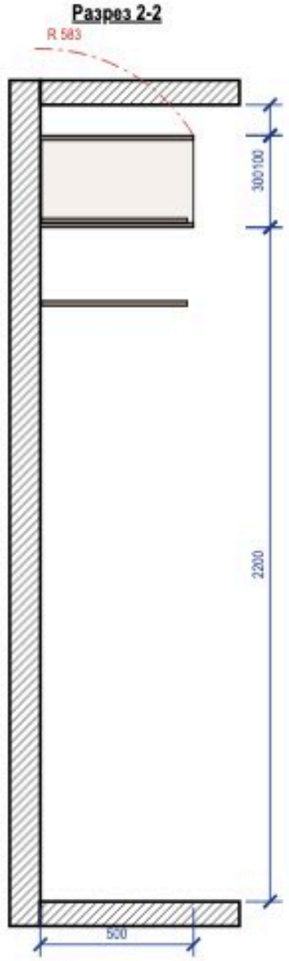

Примечания

1. Размеры — в мм по чистовой отделке; изделие 1060×500×300 (Ш×Г×В). Перед раскроем — контрольный замер цеха после чистовой отделки стен, пола и потолка.
2. Корпус — ЛДСП 16 мм, задняя стенка ХДФ 4 мм в паз, цоколь 0 мм на регулируемых опорах; открытая система без фасадов, ящики с фасадами.
3. Кромка: скрытые торцы 0,4 мм, видимые 2 мм (ПВХ/АБС).
4. Номинальные зазоры: между фасадами ящиков 3 мм, фасад ящика — стойка 2 мм.
5. Ящики — направляющие полного выдвижения NL 450 (внутренняя глубина 496 мм ≥ NL + 3); присадка по 32-й системе — выполняет цех.
6. Зазор до потолка 100 мм — закрыть планкой в цвет корпуса при монтаже.
7. Подъём корпуса (траектория на виде — красная: корпус не проходит под потолком): диагональ боковины $\sqrt{(300^2 + 500^2)} = 583$ мм > 400 мм до потолка — поднять собранный корпус нельзя: высота корпуса не более 0 мм, остальное — компенсатор, либо сборка стоя на месте.
8. Крепление к стене от опрокидывания: крепление к стене, 4 точки; основание стены и шаг анкеров — монтажная схема шкафов.
9. Проход перед изделием 450 мм показан на разрезе 1-1: меньше 600 мм — глубину уменьшить (торцевые штанги при глубине 350–450 мм) или изменить расстановку.


3D орто

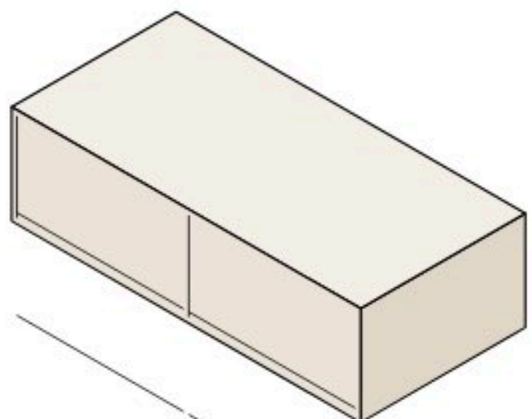


					Проект: Четырёхкомнатная квартира	
	Лист	№ док.	Подпись	Дата		
Дизайнер	Кырпан А.С.			05.10.26	Система хранения M_32	Стадия: П; Лист: Д_9; Листов: 111

выпуск 05.10.2026 d0efc1af8a · стр. 102 из 111


Вид с фасадами

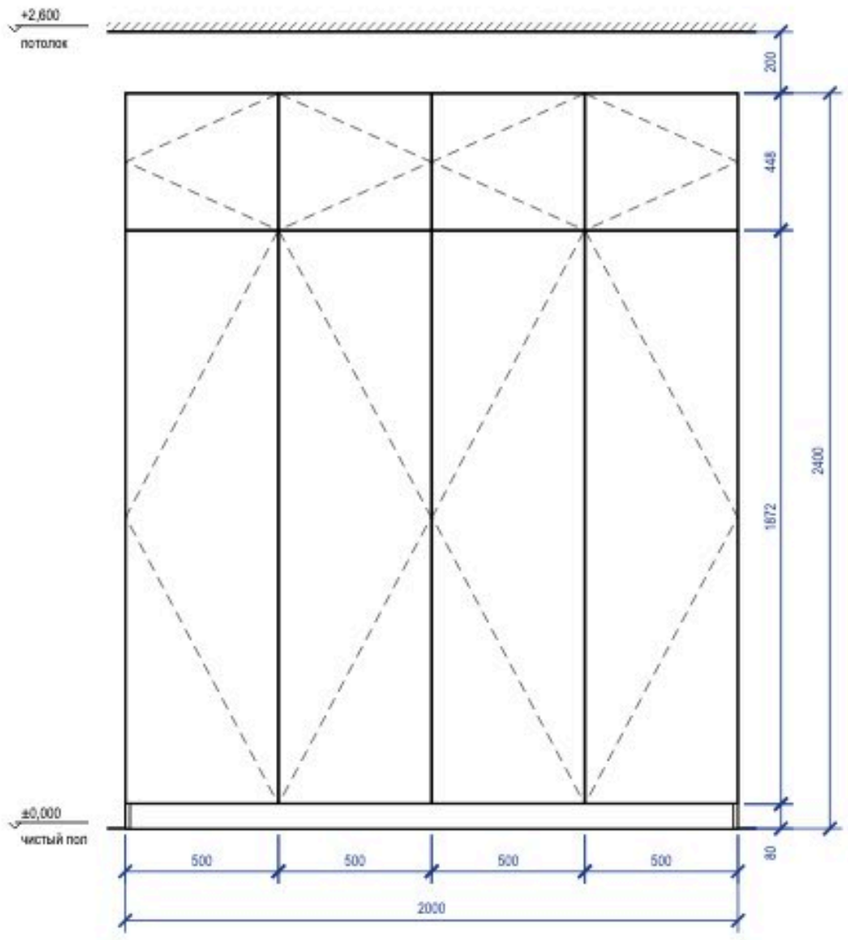


Вид без фасадов

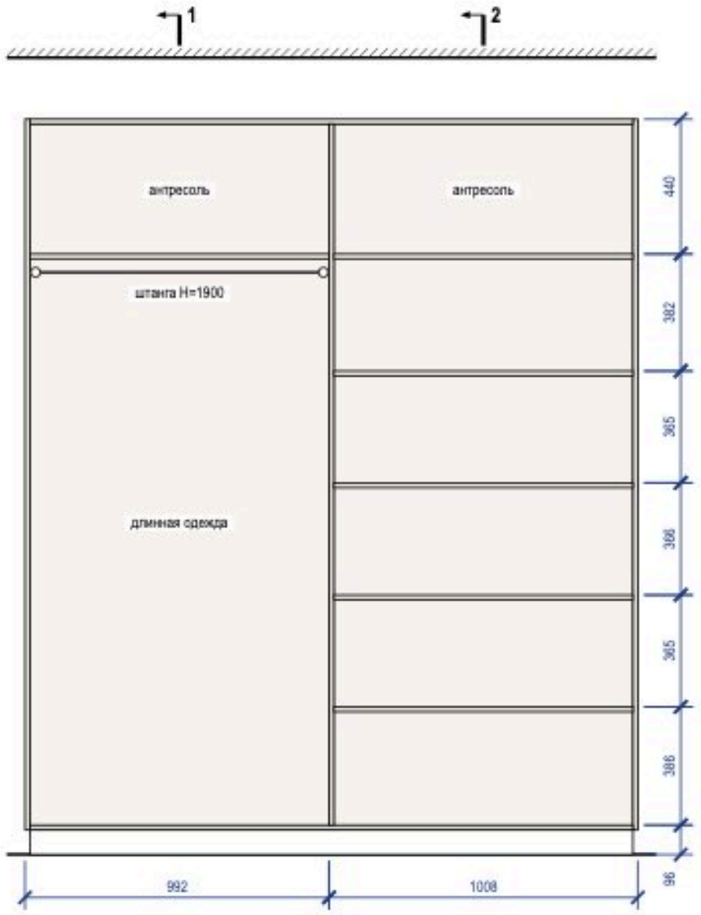

Разрез 1-1

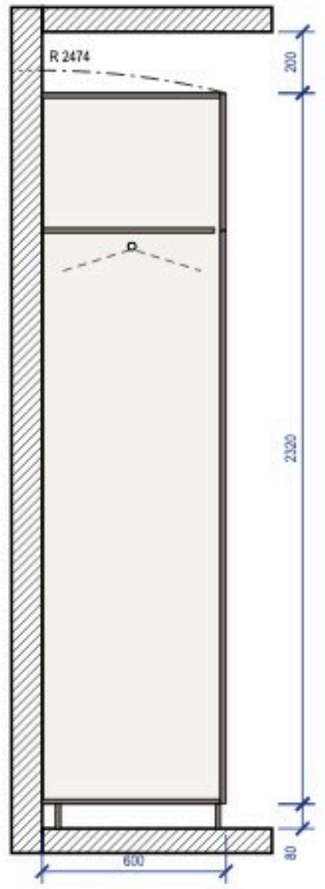


Разрез 2-2

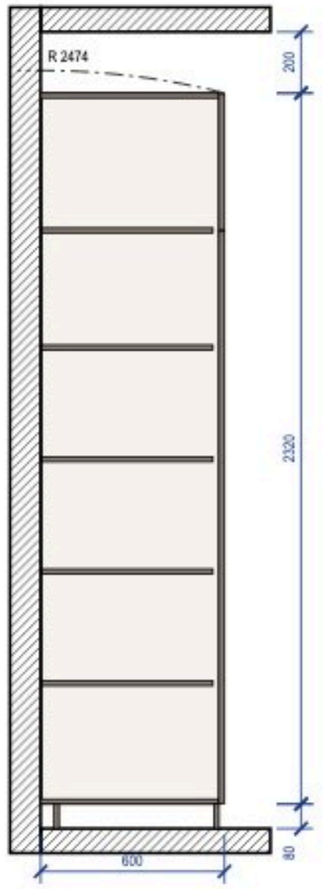

Примечания

1. Размеры — в мм по чистовой отделке; изделие 2000×600×2400 (Ш×Г×В). Перед раскроем — контрольный замер цеха после чистовой отделки стен, пола и потолка.
2. Корпус — ЛДСП 16 мм, задняя стенка ХДФ 4 мм в паз, цоколь 80 мм на регулируемых опорах; фасады — МДФ, эмаль матовая 18 мм накладные, цвет — по колерной карте; петли с доводчиком: фасад 1869 мм — 4 петли, фасад 445 мм — 2 петли.
3. Кромка: скрытые торцы 0,4 мм, видимые 2 мм (ПВХ/АБС).
4. Номинальные зазоры: между фасадами 3 мм, фасад — стена и фасад — потолок не менее 3 мм, фасад ящика — стойка 2 мм.
5. Ящики — направляющие полного выдвижения NL 550 (внутренняя глубина 578 мм ≥ NL + 3); присадка по 32-й системе — выполняет цех.
6. Зазор до потолка 200 мм.
7. Подъём корпуса: диагональ боковины $\sqrt{(2400^2 + 600^2)} = 2474$ мм < 2600 мм до потолка — корпус собирается лёжа и поднимается поворотом.
8. Крепление к стене от опрокидывания: уголок к стене, 3 шт.; основание стены и шаг анкеров — монтажная схема шкафов.


3D орто

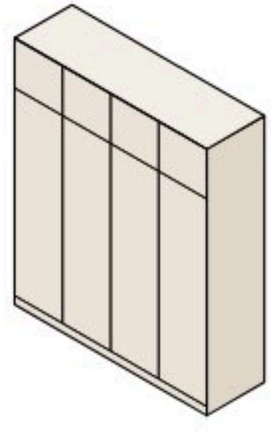


					Проект: Четырёхкомнатная квартира			
	Лист	№ док.	Подпись	Дата	Шкаф распашной М_34	Стадия	Лист	Листов
Дизайнер	Кырпан А.С.			05.10.26		П	Д_10	111

выпуск 05.10.2026 · d0efc1af8a · стр. 103 из 111


Общий вид

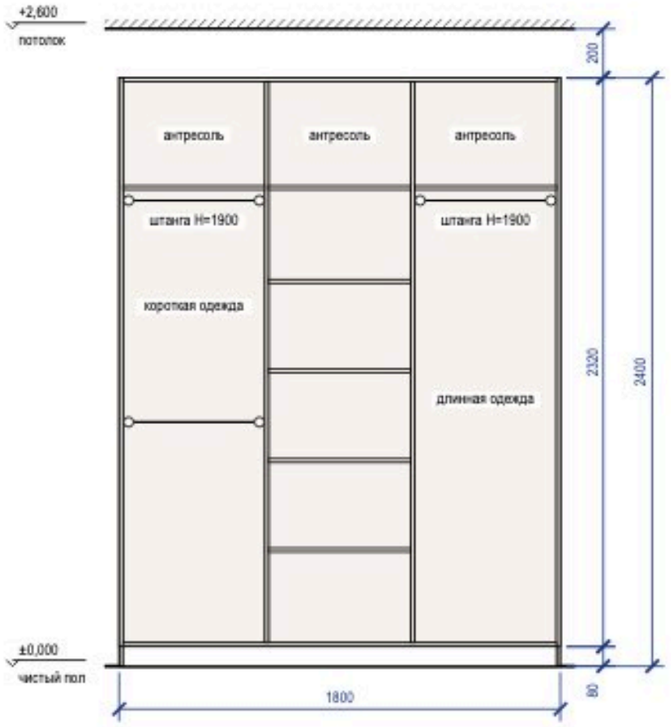


Наполнение, размеры в свету

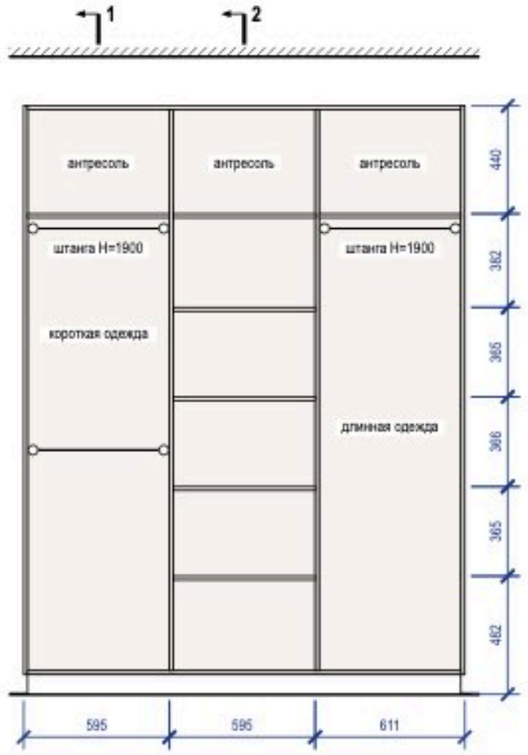

Разрез 1-1

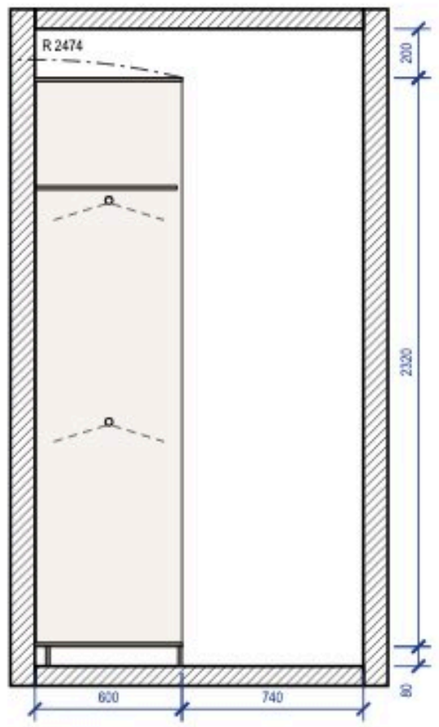


Разрез 2-2

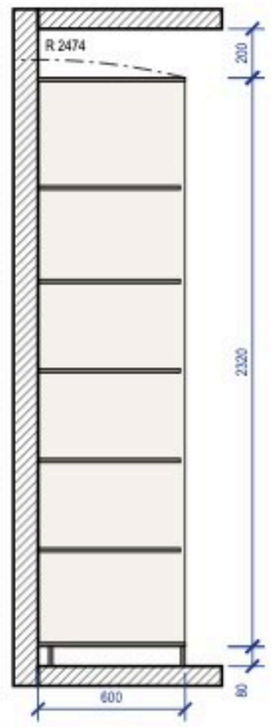

Примечания

1. Размеры — в мм по чистовой отделке; изделие 1800×600×2400 (Ш×Г×В). Перед раскроем — контрольный замер цеха после чистовой отделки стен, пола и потолка.
2. Корпус — ЛДСП 16 мм, задняя стенка ХДФ 4 мм в паз, цоколь 80 мм на регулируемых опорах; открытая система без фасадов, ящики с фасадами.
3. Кромка: скрытые торцы 0,4 мм, видимые 2 мм (ПВХ/АБС).
4. Номинальные зазоры: между фасадами ящиков 3 мм, фасад ящика — стойка 2 мм.
5. Ящики — направляющие полного выдвижения NL 550 (внутренняя глубина 596 мм ≥ NL + 3); присадка по 32-й системе — выполняет цех.
6. Зазор до потолка 200 мм.
7. Подъём корпуса: диагональ боковины $\sqrt{(2400^2 + 600^2)} = 2474$ мм < 2600 мм до потолка — корпус собирается лёжа и поднимается поворотом.
8. Крепление к стене от опрокидывания: крепление к стене, 4 точки; основание стены и шаг анкеров — монтажная схема шкафов.
9. Проход перед изделием 740 мм показан на разрезе 1-1.


3D орто

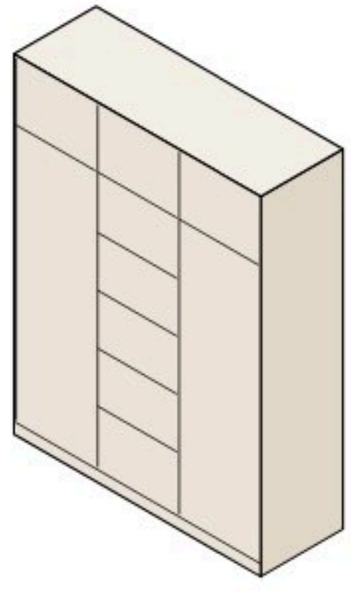


					Проект: Четырёхкомнатная квартира		
	Лист	№ док.	Подпись	Дата	Система хранения M_38	Стадия	Лист	Листов
Дизайнер	Кырпан А.С.			05.10.26		П	Д_11	111

выпуск 05.10.2026 · d0efc1af8a · стр. 104 из 111


Общий вид

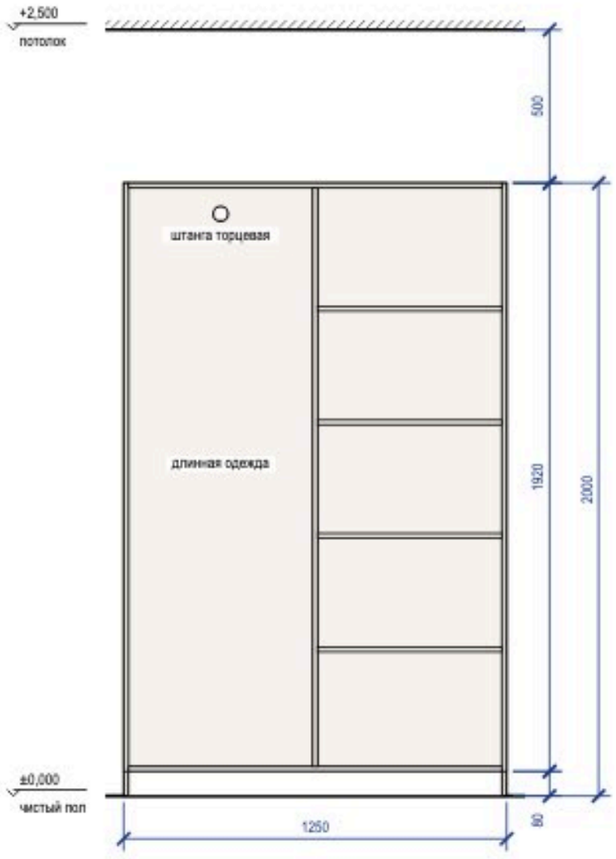


Наполнение, размеры в свету

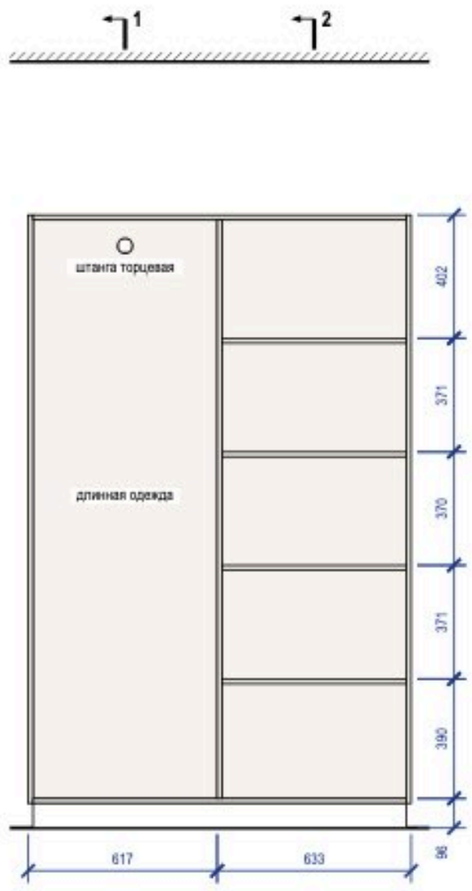

Разрез 1-1

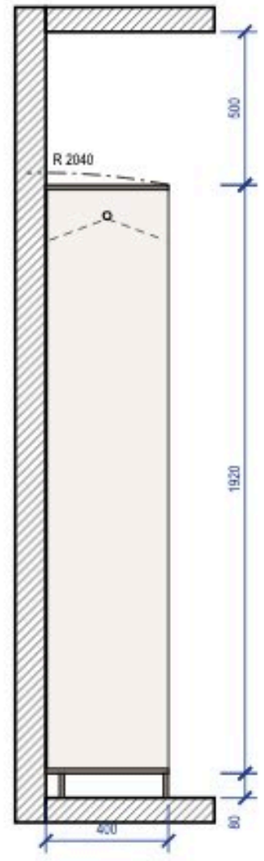


Разрез 2-2

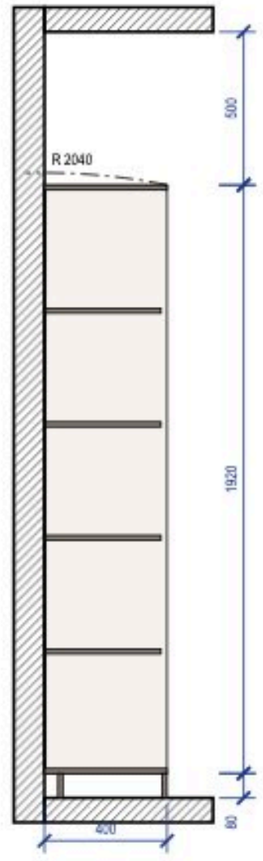

Примечания

1. Размеры — в мм по чистовой отделке; изделие 1250×400×2000 (Ш×Г×В). Перед раскроем — контрольный замер цеха после чистовой отделки стен, пола и потолка.
2. Корпус — ЛДСП 16 мм, задняя стенка ХДФ 4 мм в паз, цоколь 80 мм на регулируемых опорах; открытая система без фасадов, ящики с фасадами.
3. Кромка: скрытые торцы 0,4 мм, видимые 2 мм (ПВХ/АБС).
4. Номинальные зазоры: между фасадами ящиков 3 мм, фасад ящика — стойка 2 мм.
5. Ящики — направляющие полного выдвижения NL 350 (внутренняя глубина 396 мм ≥ NL + 3); присадка по 32-й системе — выполняет цех.
6. Зазор до потолка 500 мм.
7. Подъём корпуса: диагональ боковины $\sqrt{(2000^2 + 400^2)} = 2040$ мм < 2500 мм до потолка — корпус собирается лёжа и поднимается поворотом.
8. Крепление к стене от опрокидывания: крепление к стене, 3 точки; основание стены и шаг анкеров — монтажная схема шкафов.


3D орто

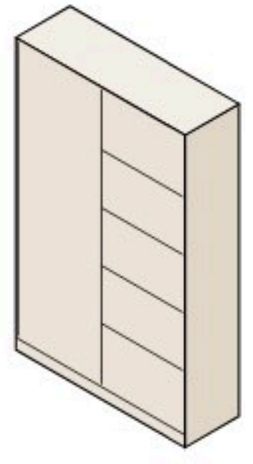


					Проект: Четырёхкомнатная квартира		
	Лист	№ док.	Подпись	Дата			
Дизайнер	Кырпан А.С.			05.10.26	Система хранения M_39	Стадия	Лист	Листов
						П	Д_12	111

выпуск 05.10.2026 № d0efc1af8a · стр. 105 из 111


Общий вид

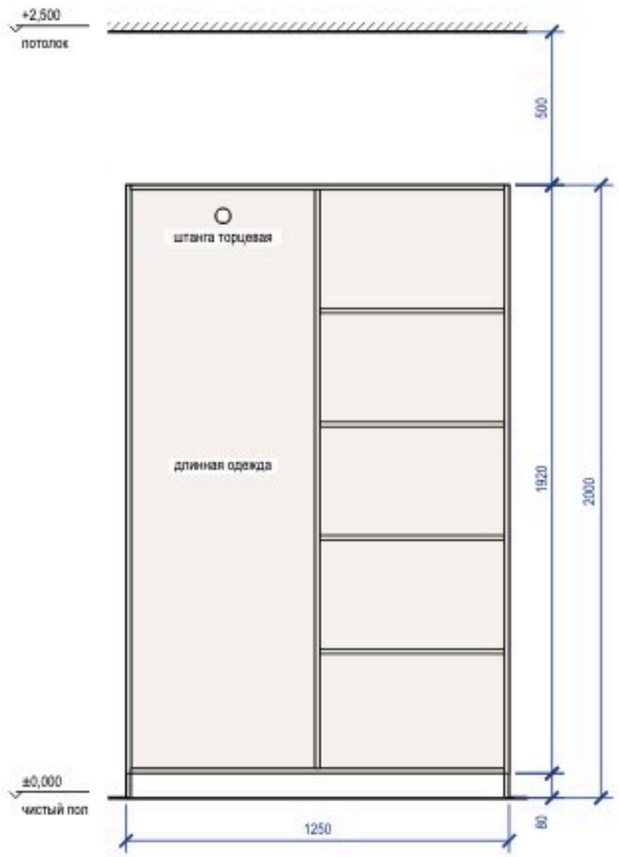


Наполнение, размеры в свету

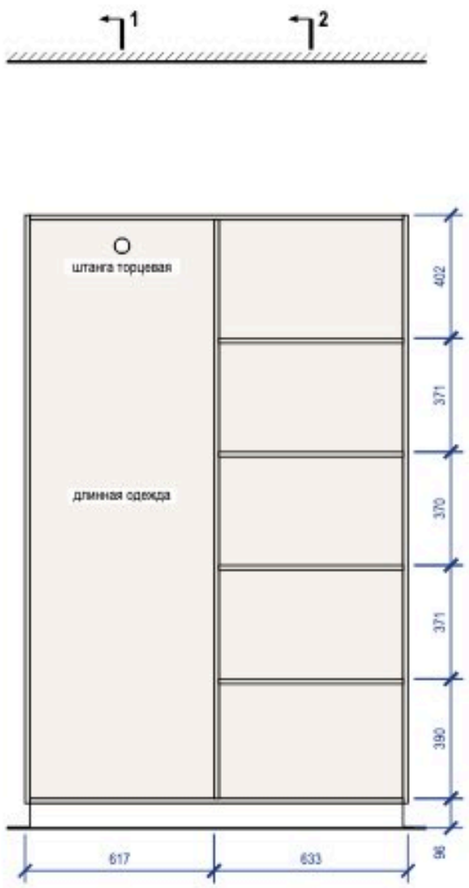

Разрез 1-1

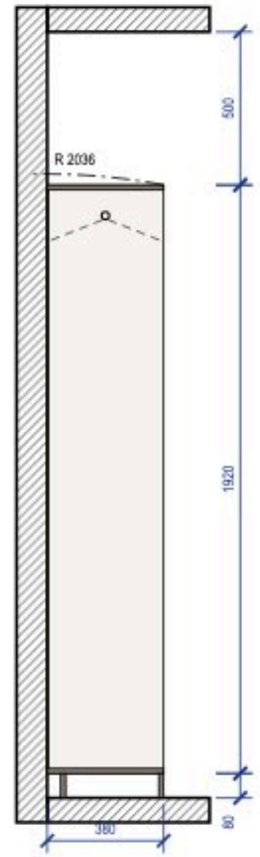


Разрез 2-2

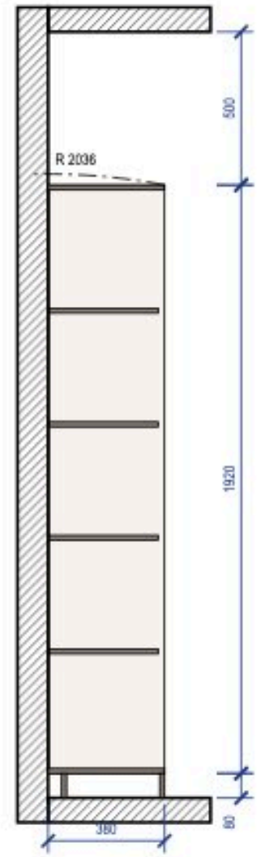

Примечания

1. Размеры — в мм по чистовой отделке; изделие 1250×380×2000 (Ш×Г×В). Перед раскроем — контрольный замер цеха после чистовой отделки стен, пола и потолка.
2. Корпус — ЛДСП 16 мм, задняя стенка ХДФ 4 мм в паз, цоколь 80 мм на регулируемых опорах; открытая система без фасадов, ящики с фасадами.
3. Кромка: скрытые торцы 0,4 мм, видимые 2 мм (ПВХ/АБС).
4. Номинальные зазоры: между фасадами ящиков 3 мм, фасад ящика — стойка 2 мм.
5. Ящики — направляющие полного выдвижения NL 350 (внутренняя глубина 376 мм ≥ NL + 3); присадка по 32-й системе — выполняет цех.
6. Зазор до потолка 500 мм.
7. Подъём корпуса: диагональ боковины $\sqrt{(2000^2 + 380^2)} = 2036$ мм < 2500 мм до потолка — корпус собирается лёжа и поднимается поворотом.
8. Крепление к стене от опрокидывания: крепление к стене, 3 точки; основание стены и шаг анкеров — монтажная схема шкафов.


3D орто

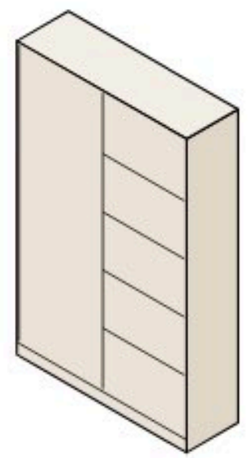


					Проект: Четырёхкомнатная квартира	
	Лист	№ док.	Подпись	Дата		
Дизайнер	Кырпан А.С.			05.10.26	Система хранения M_40	Стадия / Лист / Листов
						П / Д_13 / 111

выпуск 05.10.2026 № d0efc1af8a · стр. 106 из 111


Вид с фасадами

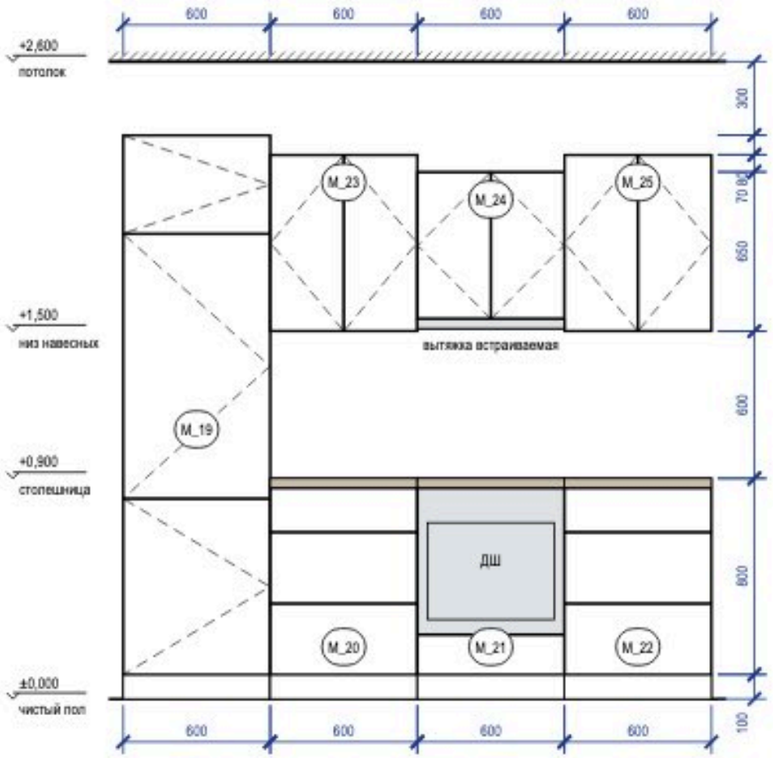


Вид без фасадов (наполнение, выводы)

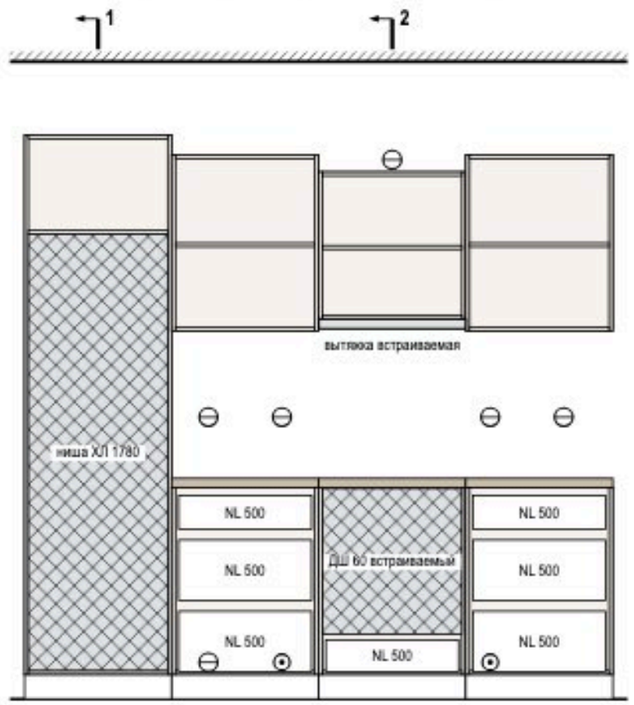


Разрез 1-1

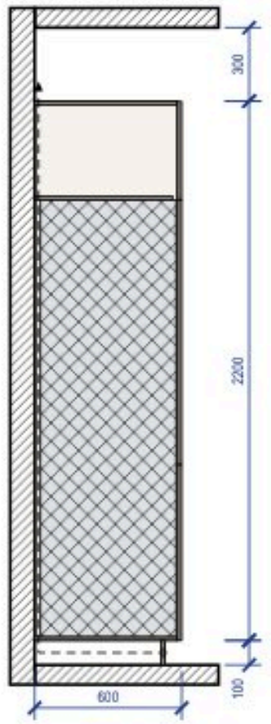

Разрез 2-2

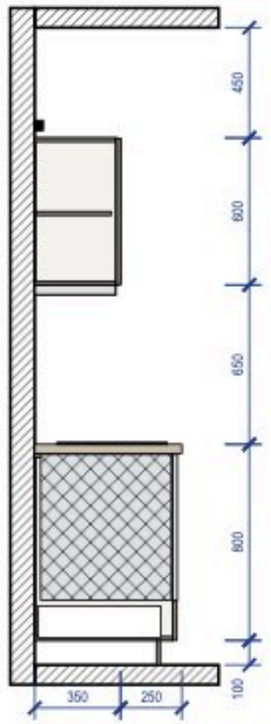

3D орто

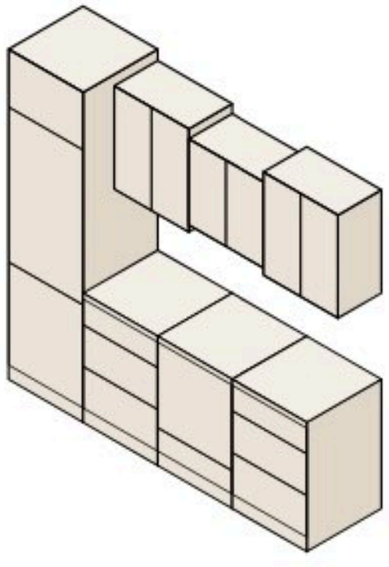


Примечания

1. Размеры — в мм по чистовой отделке, вид из помещения; марки — как на плане расстановки. Перед раскроем — контрольный замер цеха после фартука и пола.
2. Корпуса — ЛДСП 16 мм, задняя стенка ХДФ 4 мм; фасады — МДФ, эмаль матовая 18 мм, цвет по колерной карте; столешница 38 мм, свес 20 мм; цоколь 100 мм.
3. Кромка: скрытые торцы 0,4 мм, видимые 2 мм. Номинальные зазоры: между фасадами 3 мм, фасад — столешница 3 мм, фасад — стена не менее 3 мм.
4. Ящики полного выдвижения и петли — с доводчиком; присадка по 32-й системе — выполняет цех.
5. Вытяжка встраивается в навесной модуль над варочной: её низ 610 мм над панелью — меньше 650 мм, модуль поднять или принять вытяжку с допуском по паспорту модели.
6. Ниши техники (холодильник — ориентир 1780 мм) — по монтажным схемам выбранных моделей: решётка в цоколе и канал за пеналом холодильника, зазор за духовым шкафом, фасад ПММ на двери машины.


					Проект: Четырёхкомнатная квартира	
	Лист	№ док.	Подпись	Дата	Кухня (пом. 6). Развёртка гарнитура	Стадия / Лист / Листов
Дизайнер	Кырпан А.С.			05.10.26		П / Д_14 / 111

выпуск 05.10.2026 · d0efc1af8a · стр. 107 из 111


Вид с фасадами

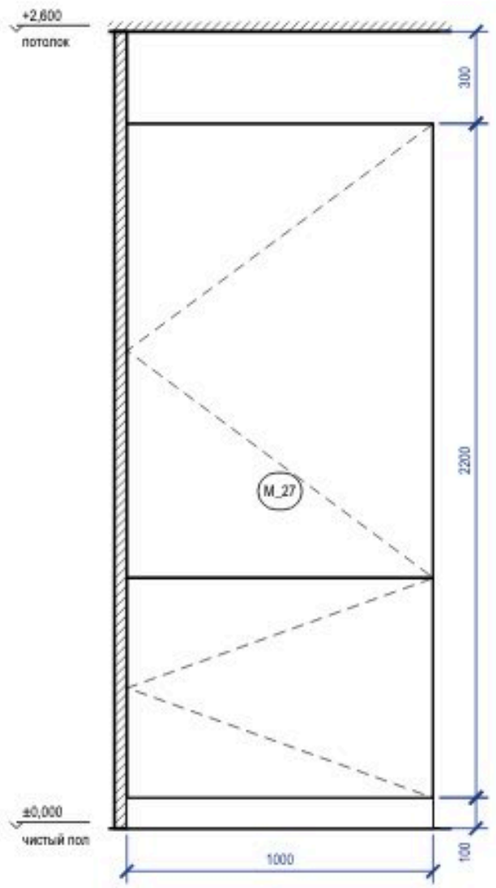


Вид без фасадов (наполнение, выводы)

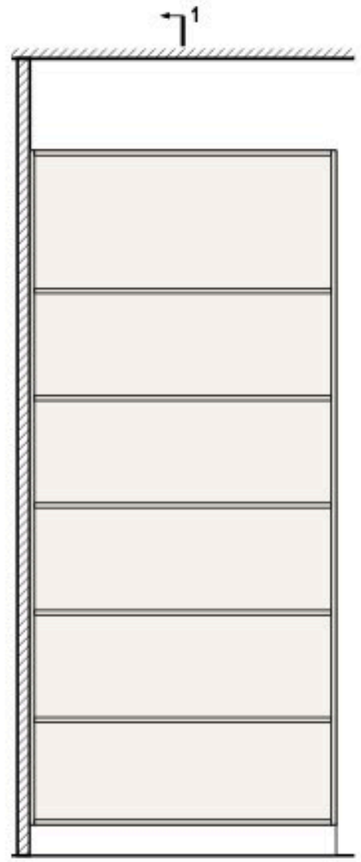

Разрез 1-1

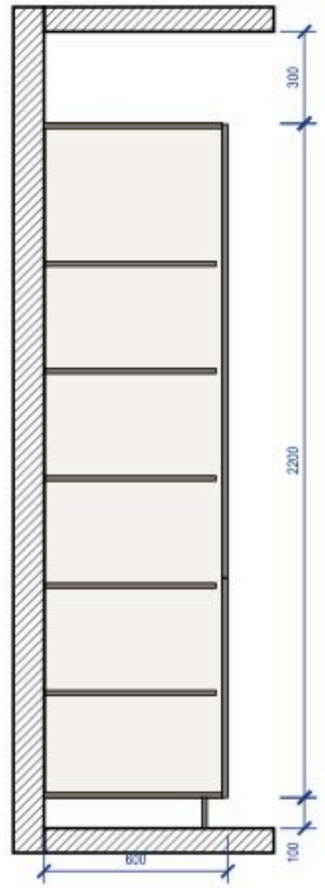

3D орто

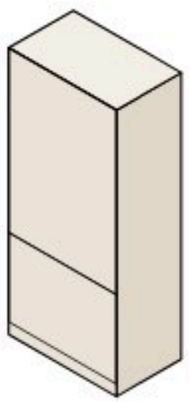

Примечания

1. Размеры — в мм по чистовой отделке, вид из помещения; марки — как на плане расстановки. Перед раскроем — контрольный замер цеха после фартука и пола.
2. Корпуса — ЛДСП 16 мм, задняя стенка ХДФ 4 мм; фасады — МДФ, эмаль матовая 18 мм, цвет по колерной карте; столешница 38 мм, свес 20 мм; цоколь 100 мм.
3. Кромка: скрытые торцы 0,4 мм, видимые 2 мм. Номинальные зазоры: между фасадами 3 мм, фасад — столешница 3 мм, фасад — стена не менее 3 мм.
4. Ящики полного выдвижения и петли — с доводчиком; присадка по 32-й системе — выполняет цех.
5. Ниши техники — по монтажным схемам выбранных моделей: решётка в цоколе и канал за пеналом холодильника, зазор за духовым шкафом, фасад ПММ на двери машины.

					Проект: Четырёхкомнатная квартира
	Лист	№ док.	Подпись	Дата	Кухня (пом. 6). Развёртка гарнитура
Дизайнер	Кырпан А.С.			05.10.26	

Стадия	Лист	Листов
П	Д_15	111

выпуск 05.10.2026 № d0efc1af8a · стр. 108 из 111

Ведомость отделки помещений (форма 1 прил. А ГОСТ 21.501-2018). Лист 1 из 2

№	Наименование помещения	Потолок			Стены и перегородки			Низ стен (плинтус)			Пол		Примечание
		Вид отделки	Код цвета	S, м²	Вид отделки	Код цвета	S, м²	Вид отделки	Код цвета	L, м	Вид отделки	S, м²	
1	Зал 18,16 м²	ГКЛ по каркасу П113, отм. +2,600; +2,600; окраска, Tikkurila Anti-Reflex 2, глубокоматовая, 2 слоя, подготовка Q3	Tikkurila F497	18,16	Окраска, Tikkurila Optiva 5 Matt, матовая, 2 слоя, подготовка К3 Акцент — стена А: окраска, Tikkurila Optiva 5 Matt, матовая, 3 слоя, подготовка К3	Tikkurila F497 Tikkurila L481	25,94 13,55	Плинтус МДФ h=80 мм, аналог: МДФ под окраску 80×16 мм	Tikkurila F497	16,6	Инженерная доска, аналог: дуб натуральный брашированный, масло-воск, 14/4 мм, на клею; тип 1, отм. ЧП ±0,000	18,16	Н стен 2500 (до потолка); колеруется в код стен, но по эмали на МДФ: сличать отдельным выкрасом на своей подложке (выкрас № 10); плинтус в цвет: стены
2	Ванная комната 5,57 м²	ГКЛВ по каркасу П113, отм. +2,500; окраска, Tikkurila Luja 7, матовая, 2 слоя, подготовка Q3	Tikkurila F497	5,57	Облицовка плиткой, аналог: керамогранит матовый, тон F497, 600×600×9 мм, клей C2 TE S1, затирка CG2WA	#F1F1EC	22,35	нет (облицовка от пола)			Аналог: керамогранит матовый R10, тон J484, 600×600×10 мм; тип 2, отм. ЧП −0,015	5,57	Н стен 2515 (до потолка); тёплый пол; гидроизоляция обмазочная, 2 слоя, по всему помещению, с заведением на стены 200 мм, в душе — на 2100 мм и 500 мм за кабину (по пирогу пола); тест проливом и акт скрытых работ; облицовка от чистого пола до низа потолка; по ГКЛВ каркаса П113, влагостойкая окраска; Q3
3	Тёмная комната 2,96 м²	ГКЛ по каркасу П113, отм. +2,600; окраска, Tikkurila Anti-Reflex 2, глубокоматовая, 2 слоя, подготовка Q3	Tikkurila F497	2,96	Окраска, Tikkurila Optiva 5 Matt, матовая, 2 слоя, подготовка К3	Tikkurila F497	16,94	Плинтус МДФ h=80 мм, аналог: МДФ под окраску 80×16 мм	Tikkurila F497	6,4	Инженерная доска, аналог: дуб натуральный брашированный, масло-воск, 14/4 мм, на клею; тип 1, отм. ЧП ±0,000	2,96	Н стен 2600 (до потолка); колеруется в код стен, но по эмали на МДФ: сличать отдельным выкрасом на своей подложке (выкрас № 10); плинтус в цвет: стены
4	Детская 1 17,51 м²	ГКЛ по каркасу П113, отм. +2,600; окраска, Tikkurila Anti-Reflex 2, глубокоматовая, 2 слоя, подготовка Q3	Tikkurila F497	17,51	Окраска, Tikkurila Joker, полуматовая, 2 слоя, подготовка К3	Tikkurila F497	40,12	Плинтус МДФ h=80 мм, аналог: МДФ под окраску 80×16 мм	Tikkurila F497	16,2	Инженерная доска, аналог: дуб натуральный брашированный, масло-воск, 14/4 мм, на клею; тип 1, отм. ЧП ±0,000	17,51	Н стен 2600 (до потолка); колеруется в код стен, но по эмали на МДФ: сличать отдельным выкрасом на своей подложке (выкрас № 10); плинтус в цвет: стены
5	Коридор 4,54 м²	ГКЛ по каркасу П113, отм. +2,600; окраска, Tikkurila Anti-Reflex 2, глубокоматовая, 2 слоя, подготовка Q3	Tikkurila F497	4,54	Окраска, Tikkurila Optiva 20 Semimatt, полуматовая, 2 слоя, подготовка К3	Tikkurila J484	22,21	Плинтус МДФ h=80 мм, аналог: МДФ под окраску 80×16 мм	Tikkurila J484	8,1	Аналог: керамогранит матовый R10, тон V486, 600×600×10 мм; тип 3, отм. ЧП ±0,000	4,54	Н стен 2600 (до потолка); колеруется в код стен, но по эмали на МДФ: сличать отдельным выкрасом на своей подложке (выкрас № 10); плинтус в цвет: стены
6	Кухня 15,19 м²	ГКЛ по каркасу П113, отм. +2,600; окраска, Tikkurila Luja 7, матовая, 2 слоя, подготовка Q3	Tikkurila F497	15,19	Окраска, Tikkurila Luja 7, полуматовая, 2 слоя, подготовка К3 Фартук кухни (стена А): облицовка керамогранитом, аналог: керамогранит матовый, тон F497, 600×600×9 мм, клей C2 TE S1, затирка CG2WA	Tikkurila F497 #F1F1EC	34,48 1,11	Плинтус МДФ h=80 мм, аналог: МДФ под окраску 80×16 мм	Tikkurila F497	13,8	Инженерная доска, аналог: дуб натуральный брашированный, масло-воск, 14/4 мм, на клею; тип 4, отм. ЧП ±0,000	15,19	Н стен 2600 (до потолка); гидроизоляция обмазочная, 2 слоя, с заведением на стены 200 мм (по пирогу пола); тест проливом и акт скрытых работ; влагостойкая полуматовая окраска (класс мокрого истирания 1 по EN 13300); категория К3 по СП 71.13330.2017, табл. 7.5; по ГКЛ каркаса П113, влагостойкая окраска; Q3 колеруется в код стен, но по эмали на МДФ: сличать отдельным выкрасом на своей подложке (выкрас № 10); плинтус в цвет: стены

Примечания

1. Ведомость продолжена на листе 2 из 2; итоги, сводка площадей и примечания — на последнем листе ведомости.

					Проект: Четырёхкомнатная квартира
	Лист	№ док.	Подпись	Дата	Ведомость отделки помещений. Лист 1 из 2
Дизайнер	Кырпан А.С.			05.10.26	

Стадия	Лист	Листов
П	С1	111

выпуск 05.10.2026 · d0efc1af8a · стр. 109 из 111

Поз.	Наименование и техническая характеристика	Тип, марка, обозначение документа	Код продукции	Поставщик	Ед. изм.	Кол.	Образец	Примечание
	Лакокрасочные материалы							
1	Краска интерьерная водно-дисперсионная акриловая для стен, матовая, класс мокрого истирания 2 по EN 13300, база A; цвет Tikkurila F497 «Paperi», колеровка машинная	Tikkurila Optiva 5 Matt		Tikkurila	л	25,2		поз. К1 колерной карты; пом. 1, 3, 8, 11, 12; S = 93,0 м² × 2 сл. × 0,12 л/м² = 22,3 л, +10 % и 0,5 л на подкраску → ≥ 25,1 л; тара 2 × 9 л + 2 × 2,7 л + 2 × 0,9 л
2	Краска интерьерная водно-дисперсионная акриловая для акцентных стен, матовая, класс мокрого истирания 2 по EN 13300, база C; цвет Tikkurila L481 «Silhouette», колеровка машинная	Tikkurila Optiva 5 Matt		Tikkurila	л	10,8		поз. К2 колерной карты; пом. 1, 11; S = 24,3 м² × 3 сл. × 0,12 л/м² = 8,7 л, +10 % и 0,5 л на подкраску → ≥ 10,1 л; тара 1 × 9 л + 2 × 0,9 л
3	Краска интерьерная водно-дисперсионная акриловая для потолков, глубокоматовая, класс мокрого истирания 2 по EN 13300, база A; цвет Tikkurila F497 «Paperi», колеровка машинная	Tikkurila Anti-Reflex 2		Tikkurila	л	22,5		поз. К3 колерной карты; пом. 1, 3, 4, 5, 7, 8, 9, 11, 12; S = 80,6 м² × 2 сл. × 0,12 л/м² = 19,3 л, +10 % и 0,5 л на подкраску → ≥ 21,8 л; тара 2 × 9 л + 1 × 2,7 л + 2 × 0,9 л
4	Краска интерьерная водно-дисперсионная акриловая для потолков, матовая, класс мокрого истирания 1 по EN 13300, база A; цвет Tikkurila F497 «Paperi», колеровка машинная	Tikkurila Luja 7		Tikkurila	л	8,1		поз. К5 колерной карты; пом. 2, 6, 10, 13; S = 25,8 м² × 2 сл. × 0,12 л/м² = 6,2 л, +10 % и 0,5 л на подкраску → ≥ 7,3 л; тара 3 × 2,7 л
5	Краска интерьерная водно-дисперсионная акриловая для стен, полуматовая, класс мокрого истирания 2 по EN 13300, база A; цвет Tikkurila F497 «Paperi», колеровка машинная	Tikkurila Joker		Tikkurila	л	18,9		поз. К6 колерной карты; пом. 4, 9; S = 69,2 м² × 2 сл. × 0,12 л/м² = 16,6 л, +10 % и 0,5 л на подкраску → ≥ 18,8 л; тара 2 × 9 л + 1 × 0,9 л
6	Краска интерьерная водно-дисперсионная акриловая для стен, полуматовая, класс мокрого истирания 2 по EN 13300, база A; цвет Tikkurila J484 «Castle», колеровка машинная	Tikkurila Optiva 20 Semimatt		Tikkurila	л	13,5		поз. К7 колерной карты; пом. 5, 7; S = 46,0 м² × 2 сл. × 0,12 л/м² = 11,0 л, +10 % и 0,5 л на подкраску → ≥ 12,6 л; тара 1 × 9 л + 1 × 2,7 л + 2 × 0,9 л
7	Краска интерьерная водно-дисперсионная акриловая для стен, полуматовая, класс мокрого истирания 1 по EN 13300, база A; цвет Tikkurila F497 «Paperi», колеровка машинная	Tikkurila Luja 7		Tikkurila	л	14,4		поз. К9 колерной карты; пом. 6, 13; S = 51,0 м² × 2 сл. × 0,12 л/м² = 12,2 л, +10 % и 0,5 л на подкраску → ≥ 14,0 л; тара 1 × 9 л + 2 × 2,7 л
8	Акрилово-уретановая эмаль на водной основе, полуглянцевая в цвет Tikkurila F497 «Paperi» — окраска плинтуса	аналог по характеристикам			л	2,3		поз. К4; пом. 1, 3, 4, 6, 8, 9, 11, 12; L = 89,2 м, S = 8,6 м² × 2 сл. × 0,12 л/м² + 10 %; продукт подобрать в веере Tikkurila
9	Акрилово-уретановая эмаль на водной основе, полуглянцевая в цвет Tikkurila J484 «Castle» — окраска плинтуса	аналог по характеристикам			л	0,5		поз. К8; пом. 5, 7; L = 16,8 м, S = 1,6 м² × 2 сл. × 0,12 л/м² + 10 %; продукт подобрать в веере Tikkurila
10	Грунтовка акриловая под окраску стен и потолков — из системы производителя краски	по системе краски			м²	390		площадь окраски стен, акцентов и потолков; 1 слой перед окраской; расход — по ТУ грунтовки
	Плитка и керамогранит							
11	Керамогранит матовый R10, тон J484, 600.8×600.8 мм	аналог по характеристикам			м²	10,47		шов 2 мм; Ванная комната, пол; Санузел, пол; по раскладке 26 шт (S = 6,88 м²), с запасом 29 шт
12	Керамогранит матовый, тон F497, 600.8×600.8 мм	аналог по характеристикам			м²	63,17		шов 2 мм; Ванная комната, стены А–Г; Ванная комната, короб инсталляции; Санузел, стены А–Г; Санузел, короб инсталляции; по раскладке 157 шт (S = 34,22 м²), с запасом 175 шт
13	Керамогранит матовый R10, тон V486, 600.8×600.8 мм	аналог по характеристикам			м²	15,88		шов 2 мм; Коридор, пол; Прихожая-коридор, пол; по раскладке 39 шт (S = 12,34 м²), с запасом 44 шт
14	Керамогранит матовый, тон F497, 600.8×600.8 мм	аналог по характеристикам			м²	1,80		шов 2 мм; Кухня, фартук (ст. А); по раскладке 4 шт (S = 1,11 м²), с запасом 5 шт
15	Керамогранит матовый R11, тон V486, водопоглощение 0,5 % (BIa), противоскольжение R11, PEI IV	аналог по характеристикам			м²	4,07		13. Балкон 1, пол; раскладка не выполнена — S = 3,70 м² + 10 %; клей и затирка — по раскладке
16	Плинтус из керамогранита пола, подрезка 80 мм, верхняя кромка с запилом 45°	аналог по характеристикам			м²	8,46		13. Балкон 1, стены; раскладка не выполнена — S = 7,69 м² + 10 %; клей и затирка — по раскладке
	Напольные покрытия							
17	Дуб натуральный брашированный, масло-воск, 14/4 мм, эмиссия E1, укладка на клей	аналог по характеристикам			м²	89,3		пом. 1, 3, 4, 6, 8, 9, 11, 12; S = 83,45 м² + 7 % (прямая укладка); к заказу — кратно упаковке
18	Клей для паркета и инженерной доски, эластичный (СМП / полиуретановый)	по рекомендации производителя доски			м²	84		площадь приклейки; расход и шпатель — по ТУ клея
	Погонажные изделия							
19	Плинтус МДФ под окраску 80×16 мм, крепление к стене, окраска в цвет Tikkurila F497	аналог по характеристикам			м	117		пом. 1, 3, 4, 5, 6, 7, 8, 9, 11, 12; L = 106,0 м (периметр без дверных проёмов) + 10 % на подрезку; в штуках — по длине планки
20	Плинтус из керамогранита пола, подрезка 80 мм, верхняя кромка с запилом 45°, h = 80 мм, крепление к стене	аналог по характеристикам			м	9		пом. 13; L = 7,7 м (периметр без дверных проёмов) + 10 % на подрезку; в штуках — по длине планки
	Смеси и материалы для облицовки							
21	Затирка для швов плитки, класс CG2WA по EN 13888	аналог: Mapei Ultracolor 133		аналог:	кг	5,7		по раскладке (a+b)/(a·b) × шов × t × 1,6 + 10 %; в т. ч. 0,1 кг — позиции раскладки без марки
22	Клей плиточный C2 TE S1 по EN 12004, слой 5 мм	аналог: Litokol K80 Eco		аналог:	кг	434		18 меш. по 25 кг; 1,5 кг/м² на 1 мм слоя + 10 %; в т. ч. 10 кг — позиции раскладки без марки
23	Гидроизоляция обмазочная мокрых зон: пол, стены по периметру, зоны замачивания; 2 слоя с армирующей лентой в углах	аналог по характеристикам			м²	16,2		площадь по листу раскладки плитки + 10 %; расход смеси — по ТУ
24	Лента демпферная по периметру пола из плитки	аналог по характеристикам			м	29,1		периметр без дверных проёмов + 10 %

Примечания


1. Количества — из геометрии проекта: площади поверхностей по чистым граням стен до отделки (те же, что в ведомости отделки и колерной карте); плитка, клей и затирка — по раскладке плиточника; в графе «Кол.» — к заказу, с запасом.
2. Краска: расход 0,12 л/м² на слой в 2 слоя, если по ТУ не задан иной; запас 10 % и 0,5 л на подкраску каждого кода. Один код — одна партия, колеровка машинная в колеровочном центре бренда; в заказ — только после утверждения выкраса (колерная карта). Фасовка — по каталогу бренда на дату выпуска; к заказу — не меньше расчётного объёма.
3. «Аналог по характеристикам» — допускается изделие другого производителя с характеристиками не ниже указанных, по согласованию с автором проекта.
4. Графы «Код продукции» и «Масса 1 ед.» не заполнены: коды по классификатору продукции не присвоены, масса единицы до 25 кг (ГОСТ 21.110-2013).
5. Грунтовка и клей для доски указаны площадью обработки; объём — по ТУ выбранного продукта.

					Проект: Четырёхкомнатная квартира
	Лист	№ док.	Подпись	Дата	Спецификация отделочных материалов
Дизайнер	Кырпан А.С.			05.10.26	

Стадия	Лист	Листов
П	С2	111

1 Порог 15 мм: мокрая зона — жилое помещение (М 1:5)

Применение: двери

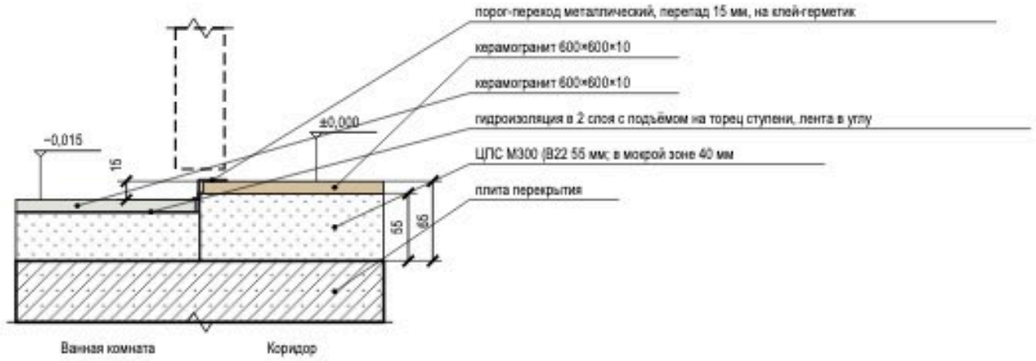


2 Стык покрытий пола Т-профилем без перепада (М 1:5)

Применение: проёмы 3↔5, 4↔5, 6↔7, 7↔8, 8↔7, 9↔7




3 Короб стояков К1-1, В1-1, Т3-1 с люком и звукоизоляцией (М 1:20)

Применение: пом. 9

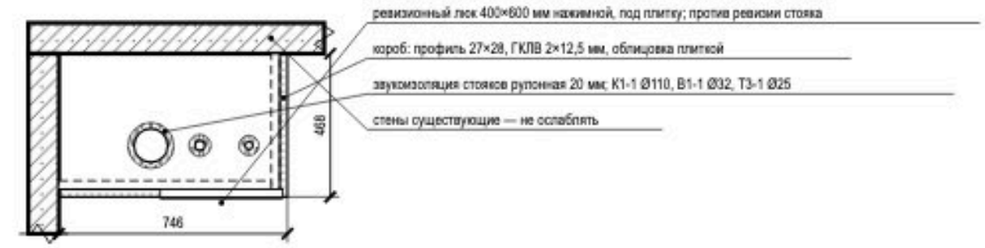


4 Гидроизоляция санузла: заход на стены 200 мм, примыкание ванны (М 1:20)

Применение: пом. 2, 10

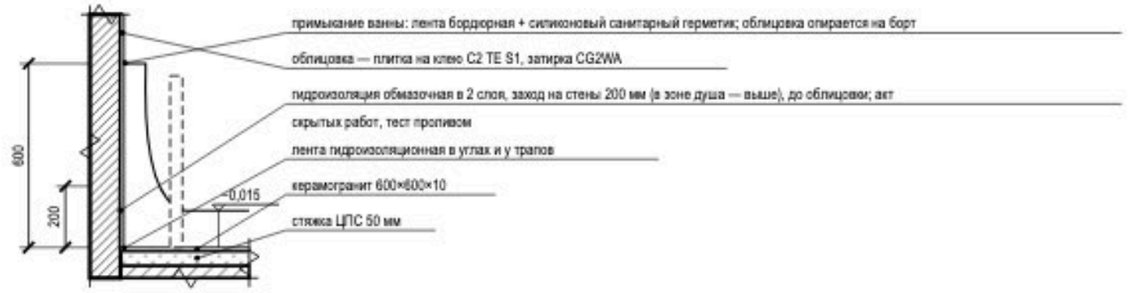

5 Плинтус МДФ 80×16 мм у окрашенной стены (М 1:10)

Применение: пом. 1, 3, 4, 5, 6, 7, 8, 9, 11, 12

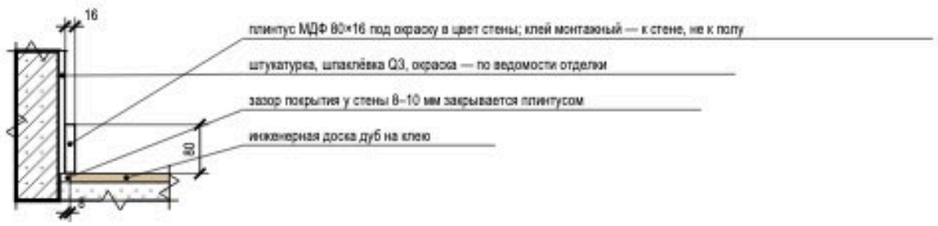

Условные обозначения

- железобетон (плита, стены)
- кладка, перегородка
- стяжка, раствор
- гипсокартон ГКЛВ
- звукоизоляция, эластичный заполнитель
- плитка, керамогранит на клею
- инженерная доска (покрытие пола)
- металлический профиль (порог, Т-профиль, короб двери)
- гидроизоляция (обмазочная, лента)

Примечания

1. Узлы — типовые решения проекта для мест, отмеченных выносками на листе схемы расположения развёрток и узлов; размеры — в мм, отметки — в м от ±0,000.
2. Узлы с гидроизоляцией, закладными и коробами скрытого монтажа принимаются по актам скрытых работ до закрытия отделкой; гидроизоляция — после теста проливом (24 ч).
3. Марки изделий (порог, Т-профиль, короб скрытой двери, люк) — по спецификациям; замена — на аналог с теми же габаритами по согласованию с автором проекта.

					Проект: Четырёхкомнатная квартира
	Лист	№ док.	Подпись	Дата	
Дизайнер	Кырпан А.С.			05.10.26	Узлы

Стадия	Лист	Листов
П	С3	111

выпуск 05.10.2026 · d0efc1af8a · стр. 111 из 111