ДИЗАЙН-ПРОЕКТ ИНТЕРЬЕРА

# Дом 120 м²

## *Средиземноморский*

**147,36 м²**

солнце и воздух · морская свежесть · неторопливость · тёплая простота · жизнь на террасе

Средиземноморский 60 % + скандинавский (scandinavian.json) 40 %: дом у соснового бора, светлый и солнечный. Стены — кремовый белый Calla G503 и известковый Wimborne White No. 239, потолки — Loft White No. 222; второй план светлый песок S 1010-Y20R, морская лазурь Lulworth Blue No. 89, серо-оливковая листва Treron No. 292; акценты эгейский синий S 3050-R80B, охра India Yellow No. 66, олива S 5020-G90Y. По брифу: дерево — дуб табак (мебель, лестница), фурнитура и светильники — латунь, рамы и металл — тёплый графит; свет тёплый 2700–3000 K, фасады матовые.

ПАЛИТРА 60 / 30 / 10

| G503 | F&B No. 239 | Little Greene No. 222 | NCS S 1010-Y20R | F&B No. 89 |
|---|---|---|---|---|
| 60 % | 60 % | 60 % | 30 % | 30 % |

АВТОР ПРОЕКТА

Кырлан Александр Сергеевич

Октябрь 2026

место под визуализацию: вид сверху (3D) с мебелью, текстилем и декором

Визуализация «вид сверху» — в работе

| ОБЪЕКТ | ОБЩАЯ ПЛОЩАДЬ | ПОМЕЩЕНИЙ |
|---|---|---|
| Дом 120 м² | 147,36 м² | 13, из них жилых 5 |
| **СТИЛЬ** | **СТАДИЯ** | **ШИФР** |
| Средиземноморский | Рабочий проект | ГД-2026-012-АИ |

| | Лист | № док. | Подпись | Дата | Проект: Дом 120 м² | | | |
|---|---|---|---|---|---|---|---|---|
| Дизайнер | Кырлан А.С. | | | 19.10.26 | Титульный лист | Стадия | Лист | Листов |
| | | | | | | П | 1 | 104 |

выпуск 19.10.2026 № 46d0102a0d · стр. 1 из 104

## Список листов



| Лист | Наименование |
|---|---|
| 1 | Титульный лист |
| 2 | Список листов |
| 3 | План планировки от заказчика · 1-й этаж |
| 4 | План планировки от заказчика · 2-й этаж |
| 5 | План монтажный · 1-й этаж |
| 6 | План монтажный · 2-й этаж |
| 7 | Кухня (пом. 1). Монтажная схема |
| 8 | Кухня (пом. 1). Монтажная схема |
| 9 | Шкафы. Монтажная схема. Лист 1 из 2 |
| 10 | Шкафы. Монтажная схема. Лист 2 из 2 |
| 11 | Карта покрытий стен · 1-й этаж |
| 12 | Карта покрытий стен · 2-й этаж |
| 13 | Колерная карта · 1-й этаж |
| 14 | Колерная карта · 2-й этаж |
| 15 | План размещения мебели и оборудования · 1-й этаж |
| 16 | План размещения мебели и оборудования · 2-й этаж |
| 17 | Спецификация мебели и оборудования |
| 18 | Спецификация мебели и оборудования (продолжение) |
| 19 | Спецификация мебели и оборудования (продолжение) |
| 20 | Ведомости изделий, техники и фурнитуры |
| 21 | План выводов сантехники · 1-й этаж |
| 22 | План выводов сантехники · 2-й этаж |
| 23 | Схема разводки водопровода и канализации · 1-й этаж |
| 24 | Схема разводки водопровода и канализации · 2-й этаж |
| 25 | Спецификация сантехнического оборудования |
| 26 | Раскладка плитки. Санузел гостевой. Развёртки стен |
| 27 | Раскладка плитки. Санузел второго этажа. Развёртки стен |
| 28 | План размещения дверей · 1-й этаж |
| 29 | План размещения дверей · 2-й этаж |
| 30 | Лестница Л-1 |
| 31 | План потолков · 1-й этаж |
| 32 | План потолков · 2-й этаж |
| 33 | План розеток и электровыводов · 1-й этаж |
| 34 | План розеток и электровыводов · 2-й этаж |
| 35 | План слаботочных сетей · 1-й этаж |
| 36 | План слаботочных сетей · 2-й этаж |
| 37 | План освещения · 1-й этаж |
| 38 | План освещения · 2-й этаж |
| 39 | Спецификация светильников и сценарии освещения |
| 40 | Управление светильниками · 1-й этаж |
| 41 | Управление светильниками · 2-й этаж |
| 42 | План вентиляции · 1-й этаж |
| 43 | План вентиляции · 2-й этаж |
| 44 | План отопления · 1-й этаж |
| 45 | План отопления · 2-й этаж |
| 46 | План покрытий пола · 1-й этаж |
| 47 | План покрытий пола · 2-й этаж |
| 48 | Раскладка плитки. Планы полов |
| 49 | Раскладка плитки. Прихожая. Фартук кухни |
| 50 | Развёртка стены А. Гостиная-кухня (пом. 1), кухонный фронт |
| 51 | Развёртка стены Б. Гостиная-кухня (пом. 1), кухонный фронт |
| 52 | Развёртка стены В. Гостиная-кухня (пом. 1) |
| 53 | Развёртка стены Г. Гостиная-кухня (пом. 1) |
| 54 | Развёртка стены А. Холл с лестницей (пом. 2) |
| 55 | Развёртка стены В. Холл с лестницей (пом. 2) |
| 56 | Развёртка стены Г. Холл с лестницей (пом. 2) |
| 57 | Развёртка стены А. Кабинет (пом. 3) |
| 58 | Развёртка стены Б. Кабинет (пом. 3) |
| 59 | Развёртка стены В. Кабинет (пом. 3) |
| 60 | Развёртка стены Г. Кабинет (пом. 3) |
| 61 | Развёртки стен А, Б. Санузел гостевой (пом. 4) |
| 62 | Развёртки стен В, Г. Санузел гостевой (пом. 4) |
| 63 | Развёртка стены А1. Прихожая (пом. 5) |
| 64 | Развёртка стены А2. Прихожая (пом. 5) |
| 65 | Развёртка стены Б. Прихожая (пом. 5) |
| 66 | Развёртка стены В. Прихожая (пом. 5) |
| 67 | Развёртки стен Г1, Г2. Прихожая (пом. 5) |
| 68 | Развёртка стены А. Спальня родителей (пом. 6) |
| 69 | Развёртка стены Б. Спальня родителей (пом. 6) |
| 70 | Развёртка стены В. Спальня родителей (пом. 6) |
| 71 | Развёртка стены Г. Спальня родителей (пом. 6) |
| 72 | Развёртка стены А. Детская (пом. 7) |
| 73 | Развёртка стены Б. Детская (пом. 7) |
| 74 | Развёртка стены В. Детская (пом. 7) |
| 75 | Развёртка стены Г. Детская (пом. 7) |
| 76 | Развёртки стен А, Б. Гардеробная (пом. 8) |
| 77 | Развёртки стен В, Г. Гардеробная (пом. 8) |
| 78 | Развёртки стен Б, В. Кладовая (пом. 9) |
| 79 | Развёртка стены Г. Кладовая (пом. 9) |
| 80 | Развёртка стены А. Холл второго этажа (пом. 10) |
| 81 | Развёртка стены В. Холл второго этажа (пом. 10) |
| 82 | Развёртка стены Г. Холл второго этажа (пом. 10) |
| 83 | Развёртки стен А, В. Коридор второго этажа (пом. 11) |
| 84 | Развёртка стены Г. Коридор второго этажа (пом. 11) |
| 85 | Развёртка стены А. Детская вторая (пом. 12) |
| 86 | Развёртка стены Б. Детская вторая (пом. 12) |
| 87 | Развёртка стены В. Детская вторая (пом. 12) |
| 88 | Развёртка стены Г. Детская вторая (пом. 12) |
| 89 | Развёртки стен А, Б. Санузел второго этажа (пом. 13) |
| 90 | Развёртки стен В, Г. Санузел второго этажа (пом. 13) |
| Д_1 | Шкаф-купе М_25 |
| Д_2 | Шкаф распашной М_30 |
| Д_3 | Шкаф распашной М_35 |
| Д_4 | Система хранения М_38 |
| Д_5 | Система хранения М_39 |
| Д_6 | Система хранения М_40 |
| Д_7 | Система хранения М_41 |
| Д_8 | Шкаф распашной М_45 |
| Д_9 | Система хранения М_47 |
| Д_10 | Кухня (пом. 1). Развёртка гарнитура |
| Д_11 | Кухня (пом. 1). Развёртка гарнитура |
| С1 | Ведомость отделки помещений. Лист 1 из 2 |
| С2 | Спецификация отделочных материалов |
| С3 | Узлы |


| | | | | |
|---|---|---|---|---|
| | Лист | № док. | Подпись | Дата |
| Дизайнер | Кырлан А.О. | | | 19.10.26 |

Проект: Дом 120 м²

| Список листов | Стадия | Лист | Листов |
|---|---|---|---|
| | П | 2 | 104 |

выпуск 19.10.2026 № 46d0102a0d · стр. 2 из 104

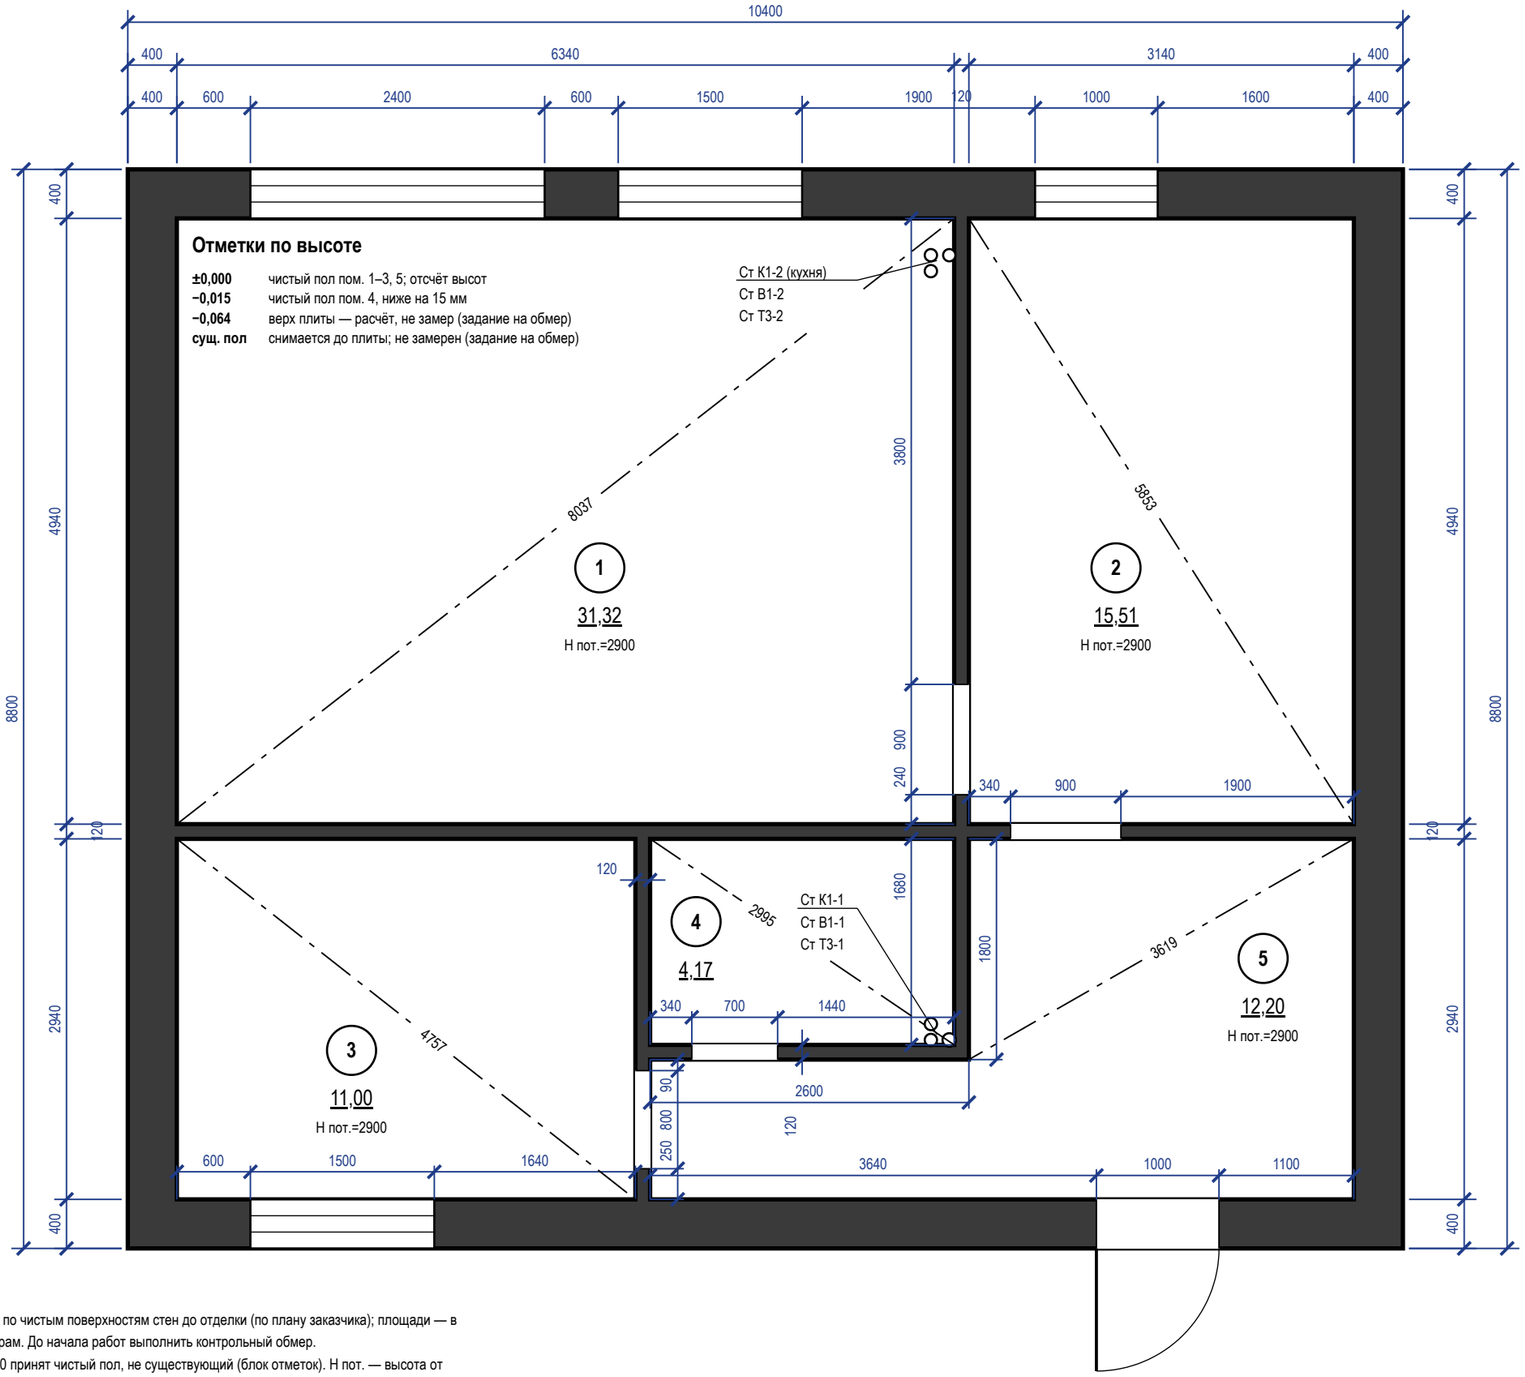


## Экспликация помещений

| № | Наименование | Площадь, м² |
|---|---|---|
| 1 | Гостиная-кухня | 31,32 |
| 2 | Холл с лестницей | 15,51 |
| 3 | Кабинет | 11,00 |
| 4 | Санузел гостевой | 4,17 |
| 5 | Прихожая | 12,20 |
| | **Итого (общая площадь)** | **147,36** |

## Условные обозначения

- существующие стены (сечение)
- окно (рама, остекление)
- проём существующий, без заполнения (откосы)
- стояк: К1 — канализация, В1 — ХВС, Т3 — ГВС
- диагональ помещения — контроль прямоугольности
- (1) номер помещения, площадь м²

## Примечания

1. Размеры — в мм по чистым поверхностям стен до отделки (по плану заказчика); площади — в м² по тем же размерам. До начала работ выполнить контрольный обмер.
2. За отметку ±0,000 принят чистый пол, не существующий (блок отметок). Н пот. — высота от чистого пола до плиты перекрытия.
3. Толщины стен: наружные 400 мм, перегородки 120 мм; отличающиеся толщины и уступы размерами на плане.
4. Несущие стены не определены: до технического заключения все стены считать несущими; проёмы и штробы в них не выполнять.
5. Дверные проёмы показаны без заполнения; высота дверных проёмов 2100 мм; низ окон (подоконник) 500, 900 мм от чистого пола, высота окон 1900, 1500 мм.
6. Диагонали — контрольные размеры; расхождение более 5 мм подписать на плане как перекос.
7. Размеры проверить на месте до начала работ; расхождение контрольных промеров ≤ 2 %.


| | Лист | № док. | Подпись | Дата |
|---|---|---|---|---|
| Дизайнер | Кырлан А.С. | | | 19.10.26 |

Проект: Дом 120 м²

План планировки от заказчика · 1-й этаж

| Стадия | Лист | Листов |
|---|---|---|
| П | 3 | 104 |

выпуск 19.10.2026 № 46d0102a0d · стр. 3 из 104

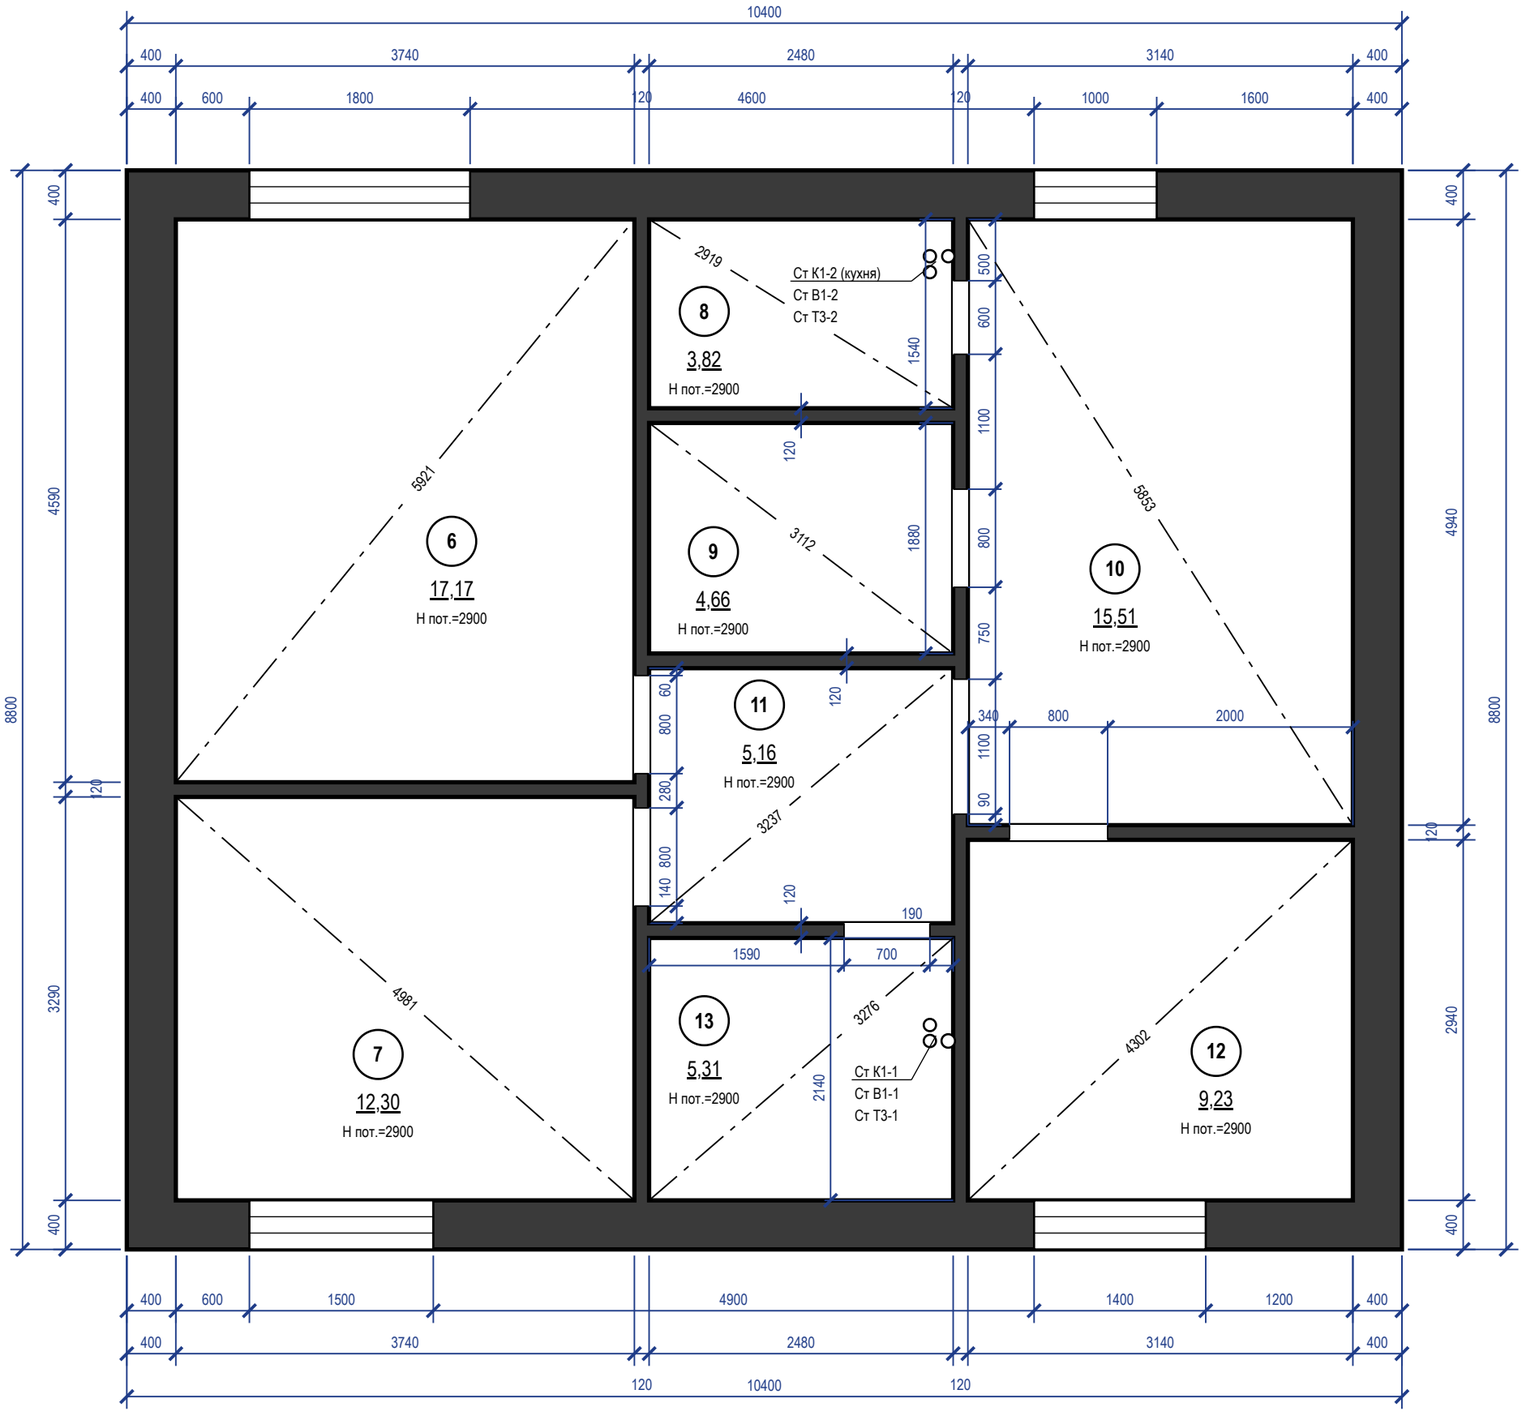


## Экспликация помещений

| № | Наименование | Площадь, м² |
|---|---|---|
| 6 | Спальня родителей | 17,17 |
| 7 | Детская | 12,30 |
| 8 | Гардеробная | 3,82 |
| 9 | Кладовая | 4,66 |
| 10 | Холл второго этажа | 15,51 |
| 11 | Коридор второго этажа | 5,16 |
| 12 | Детская вторая | 9,23 |
| 13 | Санузел второго этажа | 5,31 |
| | **Итого (общая площадь)** | **147,36** |

## Условные обозначения

- существующие стены (сечение)
- окно (рама, остекление)
- проём существующий, без заполнения (откосы)
- стояк: К1 — канализация, В1 — ХВС, Т3 — ГВС
- диагональ помещения — контроль прямоугольности
- (1) номер помещения, площадь м²

## Примечания

1. Размеры — в мм по чистым поверхностям стен до отделки (по плану заказчика); площади — в м² по тем же размерам. До начала работ выполнить контрольный обмер.
2. За отметку ±0,000 принят чистый пол, не существующий (блок отметок). Н пот. высота от чистого пола до плиты перекрытия.
3. Толщины стен: наружные 400 мм, перегородки 120 мм; отличающиеся толщины и уступы — размерами на плане.
4. Несущие стены не определены: до технического заключения все стены считать несущими; проёмы и штробы в них не выполнять.
5. Дверные проёмы показаны без заполнения; высота дверных проёмов 2100 мм, проёмов без двери 2100 мм; низ окон (подоконник) 900 мм от чистого пола, высота окон 1500, 1450 мм.
6. Диагонали — контрольные размеры; расхождение более 5 мм подписать на плане как перекос.
7. Размеры проверить на месте до начала работ; расхождение контрольных промеров ≤ 2 %.

## Отметки по высоте

| | |
|---|---|
| **±0,000** | чистый пол пом. 6–12; отсчёт высот |
| **−0,015** | чистый пол пом. 13, ниже на 15 мм |
| **−0,064** | верх плиты — расчёт, не замер (задание на обмер) |
| **сущ. пол** | снимается до плиты; не замерен (задание на обмер) |

| | | | | |
|---|---|---|---|---|
| | Лист | № док. | Подпись | Дата |
| Дизайнер | Кырлан А.С. | | | 19.10.26 |

Проект: Дом 120 м²


План планировки от заказчика · 2-й этаж

| Стадия | Лист | Листов |
|---|---|---|
| П | 4 | 104 |

выпуск 19.10.2026 № 46d0102a0d · стр. 4 из 104

## Экспликация помещений

| № | Наименование | Площадь, м² |
|---|---|---|
| 1 | Гостиная-кухня | 31,32 |
| 2 | Холл с лестницей | 15,51 |
| 3 | Кабинет | 11,00 |
| 4 | Санузел гостевой | 4,17 |
| 5 | Прихожая | 12,20 |
| | **Итого (общая площадь)** | **147,36** |

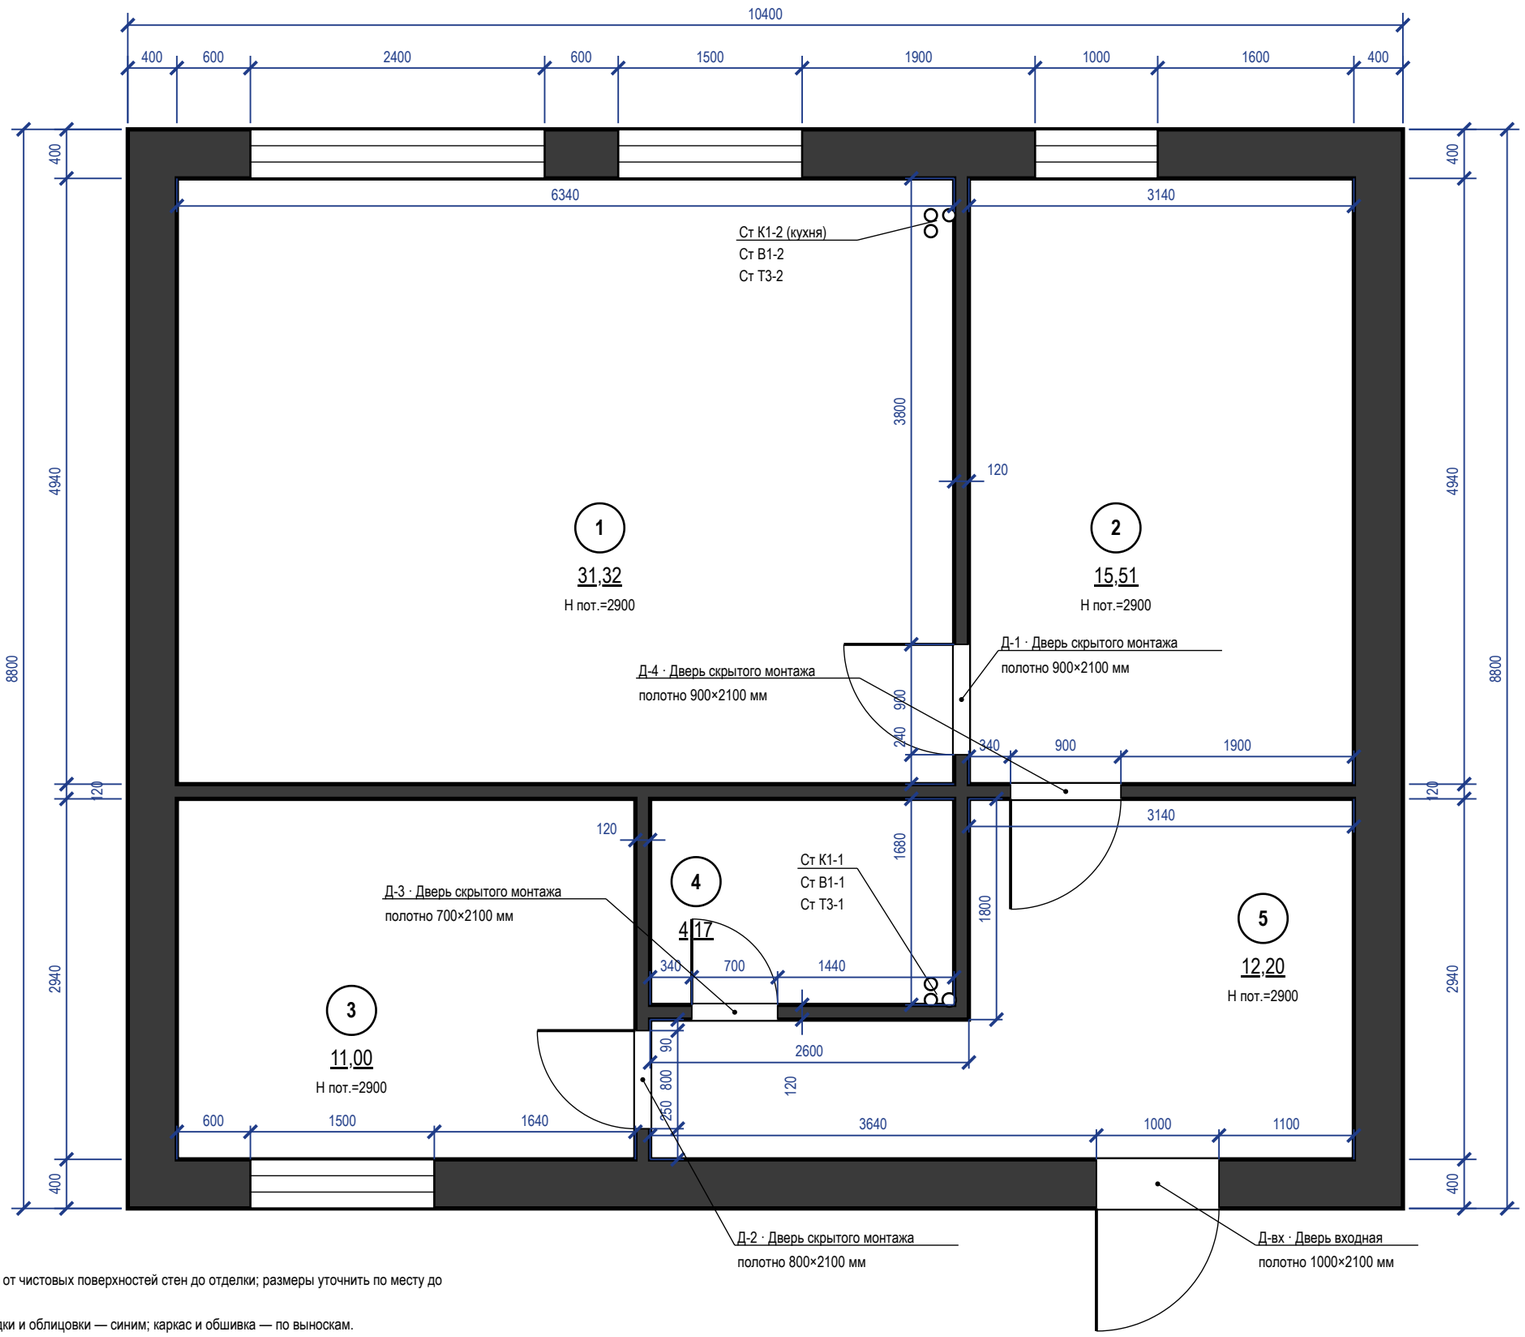



### Примечания

1. Размеры — в мм от чистовых поверхностей стен до отделки; размеры уточнить по месту до начала работ.
2. Новые перегородки и облицовки — синим; каркас и обшивка — по выноскам.
3. Несущие стены не изменять: проёмы, ниши и штробы в них — только по техническому заключению.

| | | | | | |
|---|---|---|---|---|---|
| | | | | | Проект: Дом 120 м² |
| | Лист | № док. | Подпись | Дата | План монтажный · 1-й этаж |
| Дизайнер | Кырлан А.С. | | | 19.10.26 | |

| Стадия | Лист | Листов |
|---|---|---|
| П | 5 | 104 |

выпуск 19.10.2026 № 46d0102a0d · стр. 5 из 104

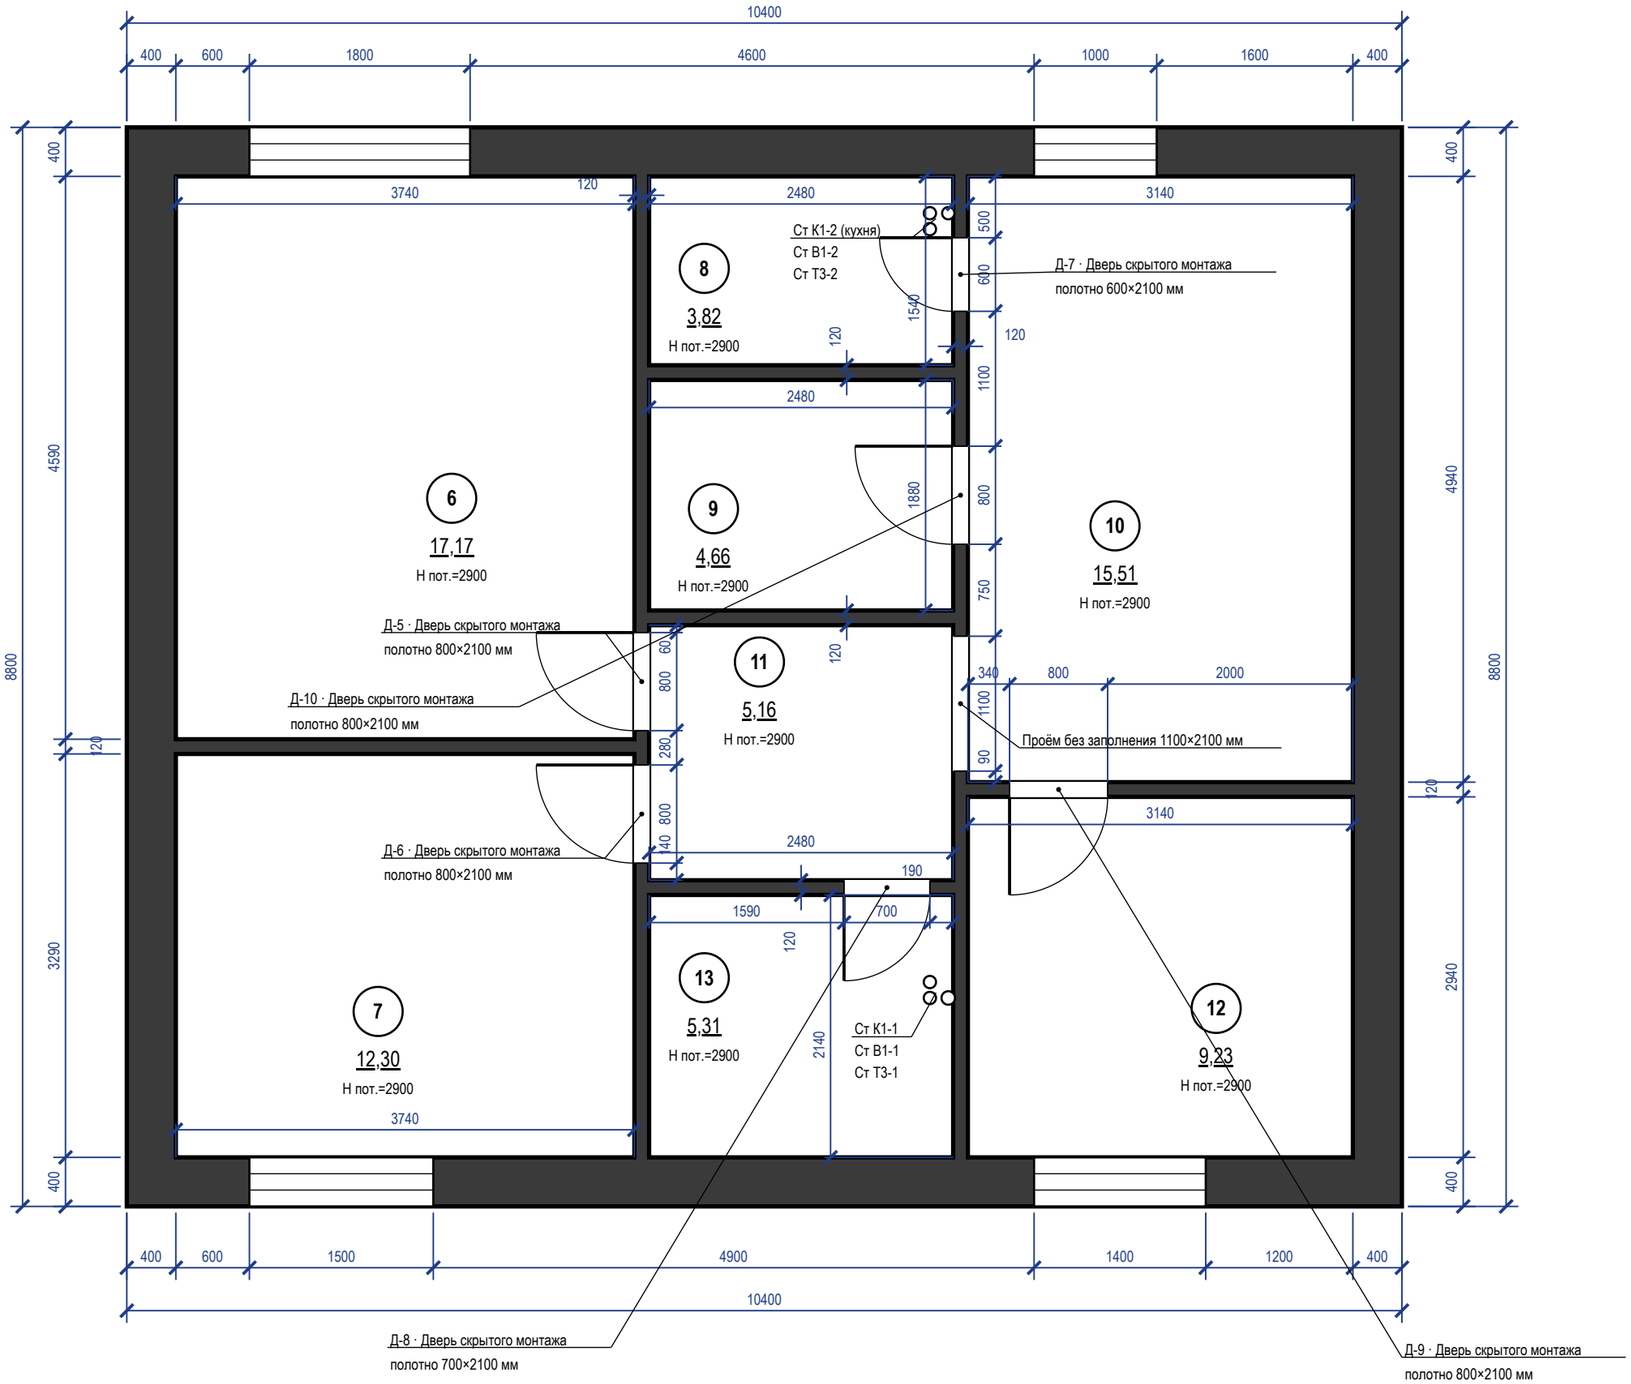


## Экспликация помещений

| № | Наименование | Площадь, м² |
|---|---|---|
| 6 | Спальня родителей | 17,17 |
| 7 | Детская | 12,30 |
| 8 | Гардеробная | 3,82 |
| 9 | Кладовая | 4,66 |
| 10 | Холл второго этажа | 15,51 |
| 11 | Коридор второго этажа | 5,16 |
| 12 | Детская вторая | 9,23 |
| 13 | Санузел второго этажа | 5,31 |
| | **Итого (общая площадь)** | **147,36** |

## Примечания


1. Размеры — в мм от чистовых поверхностей стен до отделки; размеры уточнить по месту до начала работ.
2. Новые перегородки и облицовки — синим; каркас и обшивка — по выноскам.
3. Несущие стены не изменять: проёмы, ниши и штробы в них — только по техническому заключению.

| | | | | | |
|---|---|---|---|---|---|
| | | | | | Проект: Дом 120 м² |
| | Лист | № док. | Подпись | Дата | План монтажный · 2-й этаж |
| Дизайнер | Кырлан А.С. | | | 19.10.26 | |


| Стадия | Лист | Листов |
|---|---|---|
| П | 6 | 104 |

выпуск 19.10.2026 № 46d0102a0d · стр. 6 из 104

## Привязка выводов и крепление модулей

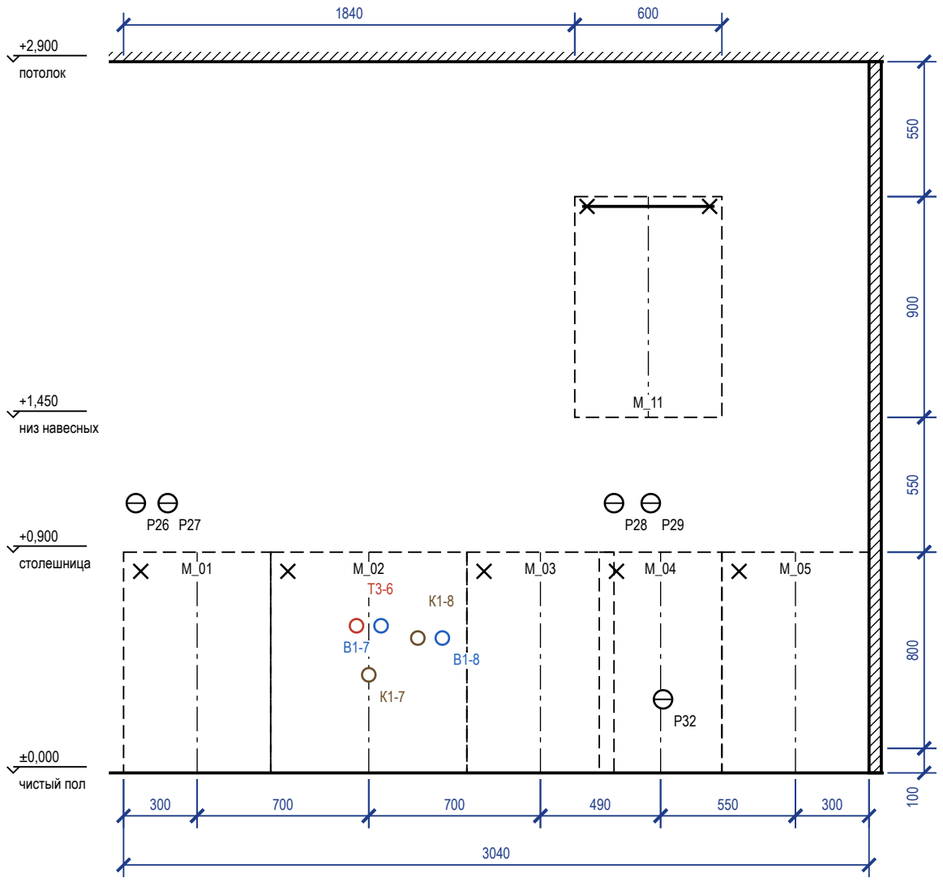


## План столешницы

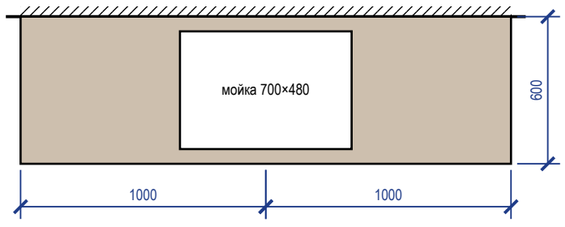


## Привязка выводов к осям модулей

| Код | Назначение | Модуль | От оси, мм | H, мм | Размещение |
|---|---|---|---|---|---|
| P26 | розетка ×2 — фартук | M_01 | −250 | 1100 | над столешницей (фартук) |
| P27 | розетка — фартук | M_01 | −120 | 1100 | над столешницей (фартук) |
| T3-6 | T3 — межос. 100 | M_02 | −50 | 600 | в модуле мойки |
| K1-7 | K1 Ø50 — мойка | M_02 | 0 | 400 | в модуле мойки |
| B1-7 | B1 — межос. 100 | M_02 | +50 | 600 | в модуле мойки |
| K1-8 | K1 Ø40 — слив ПММ в шкафу мойки | M_02 | +200 | 550 | в модуле мойки |
| B1-8 | B1 — кран ПММ в шкафу мойки | M_02 | +300 | 550 | в модуле мойки |
| P28 | розетка ×2 — фартук | M_03 | +300 | 1100 | над столешницей (фартук) |
| P29 | розетка — фартук | M_04 | −40 | 1100 | над столешницей (фартук) |
| P32 | розетка — посудомоечная машина | M_04 | +10 | 300 | в соседнем модуле, за ящиком |

## Зазоры под отделку

| Поверхность | Отделка | Зазор, мм | Учесть |
|---|---|---|---|
| фартук | керамогранит | 10 | от чернового основания до корпуса навесных и столешницы |
| стены | окраска | 5 | под штукатурку и шпаклёвку за пеналом |
| пол | инженерная доска | | цоколь — после укладки пола, опоры ±20 мм |

## Условные обозначения

- навесной модуль (невидимый контур)
- ось модуля (от неё — привязка вывода)
- анкер / уголок крепления к стене
- розетка на стене
- вывод кабеля к технике
- B1 — вывод воды B1 / T3, канализации K1

## Примечания


1. Выводы — по проекту электрики и ВК; привязка по горизонтали — от оси модуля (плюс — вправо по виду), по высоте — от чистого пола до оси вывода.
2. Пенал — уголки к стене 2 шт. сверху; нижние модули — стяжками между собой и уголком к стене; ряд выставить по уровню опорами цоколя.
3. Розетки над столешницей — не ниже 150 мм над ней и не за корпусом техники; розетка за ПММ, духовым шкафом и холодильником — только в соседнем модуле или в зоне цоколя с доступом.
4. Столешница — вырезы по шаблонам выбранных моделей мойки и варочной панели; торцы у стены — герметик, пристеночный плинтус.

| | | | | | |
|---|---|---|---|---|---|
| | | | | | Проект: Дом 120 м² |
| | Лист | № док. | Подпись | Дата | Кухня (пом. 1). Монтажная схема |
| Дизайнер | Кырлан А.С. | | | 19.10.26 | |


| Стадия | Лист | Листов |
|---|---|---|
| П | 7 | 104 |

выпуск 19.10.2026 № 46d0102a0d · стр. 7 из 104

## Привязка выводов и крепление модулей

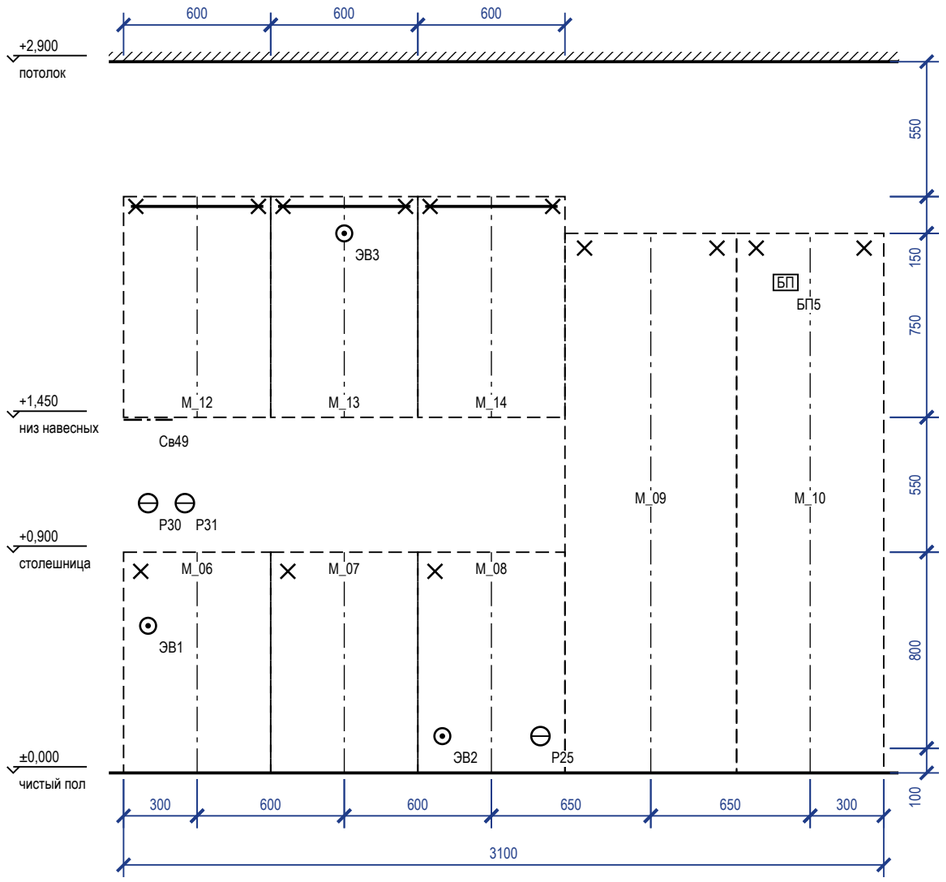


## План столешницы

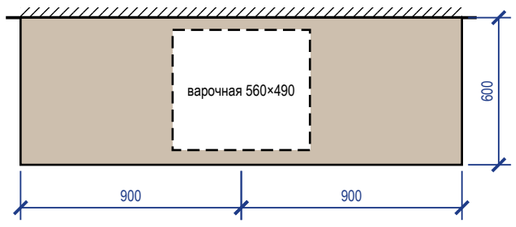


## Привязка выводов к осям модулей

| Код | Назначение | Модуль | От оси, мм | H, мм | Размещение |
|---|---|---|---|---|---|
| Р30 | розетка ×2 — фартук между мойкой и варочной | М_06 | −200 | 1100 | над столешницей (фартук) |
| ЭВ1 | вывод кабеля — варочная панель (в соседнем модуле М8.3, за ящиком) | М_06 | −200 | 600 | в соседнем модуле, за ящиком |
| Св49 | светодиодная лента — подсветка столешницы | М_06 | −200 | 1440 | в профиле по низу навесного модуля |
| Р31 | розетка — фартук между мойкой и варочной | М_06 | −50 | 1100 | над столешницей (фартук) |
| ЭВ3 | вывод кабеля — вытяжка | М_13 | 0 | 2200 | в навесном модуле |
| ЭВ2 | вывод кабеля — духовой шкаф | М_08 | −200 | 150 | в соседнем модуле, за ящиком |
| Р25 | розетка — холодильник М_09 (розетка в соседнем модуле М_08, съёмная панель) | М_08 | +200 | 150 | в соседнем модуле, за ящиком |
| БП5 | блок питания — в пенале М_32, верх, съёмная панель | М_10 | −100 | 2000 | за пеналом |

## Зазоры под отделку

| Поверхность | Отделка | Зазор, мм | Учесть |
|---|---|---|---|
| фартук | керамогранит | 10 | от чернового основания до корпуса навесных и столешницы |
| стены | окраска | 5 | под штукатурку и шпаклёвку за пеналом |
| пол | инженерная доска | | цоколь — после укладки пола, опоры ±20 мм |

## Условные обозначения

- навесной модуль (невидимый контур)
- ось модуля (от неё — привязка вывода)
- анкер / уголок крепления к стене
- розетка на стене
- вывод кабеля к технике
- B1 — вывод воды В1 / Т3, канализации К1


## Примечания

1. Выводы — по проекту электрики и ВК; привязка по горизонтали — от оси модуля (плюс — вправо по виду), по высоте — от чистого пола до оси вывода.
2. Пенал — уголки к стене 2 шт. сверху; нижние модули — стяжками между собой и уголком к стене; ряд выставить по уровню опорами цоколя.
3. Розетки над столешницей — не ниже 150 мм над ней и не за корпусом техники; розетка за ПММ, духовым шкафом и холодильником — только в соседнем модуле или в зоне цоколя с доступом.
4. Столешница — вырезы по шаблонам выбранных моделей мойки и варочной панели; торцы у стены — герметик, пристеночный плинтус.


| | | | | | |
|---|---|---|---|---|---|
| | | | | | Проект: Дом 120 м² |
| | Лист | № док. | Подпись | Дата | Кухня (пом. 1). Монтажная схема |
| Дизайнер | Кырлан А.С. | | | 19.10.26 | Стадия: П; Лист: 8; Листов: 104 |

выпуск 19.10.2026 № 46d0102a0d · стр. 8 из 104


**Шкаф-купе M_25 (пом. 5)**

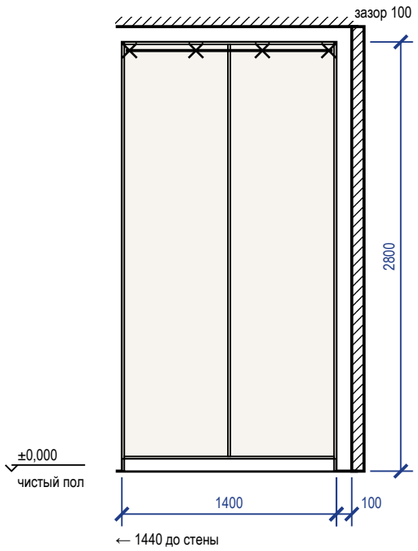



**Шкаф распашной M_30 (пом. 6)**

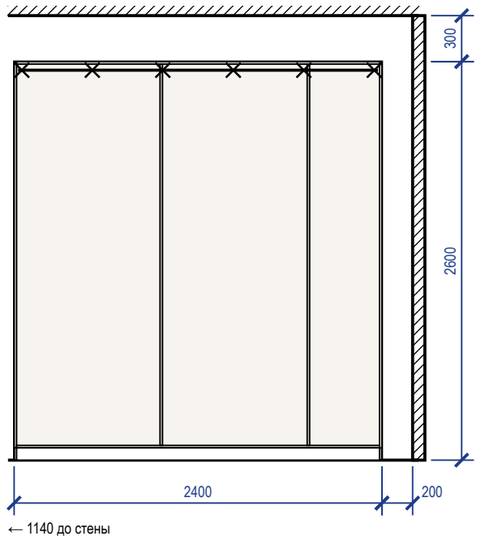



**Шкаф распашной M_35 (пом. 7)**

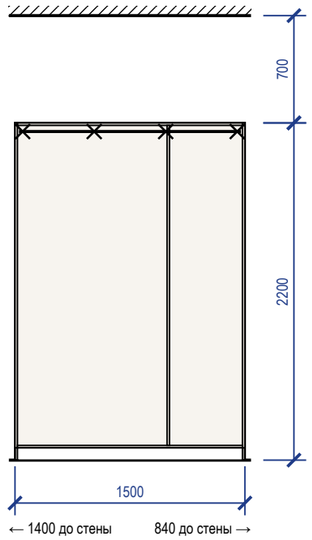


**Система хранения M_38 (пом. 8)**

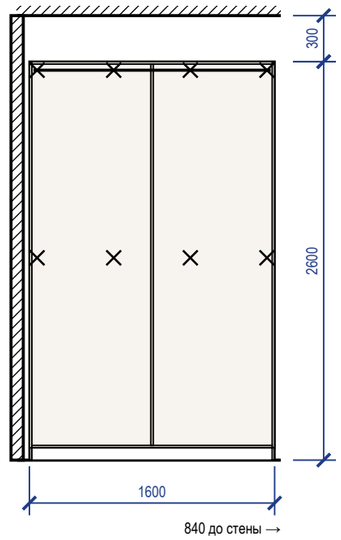


**Система хранения M_39 пом. 8**

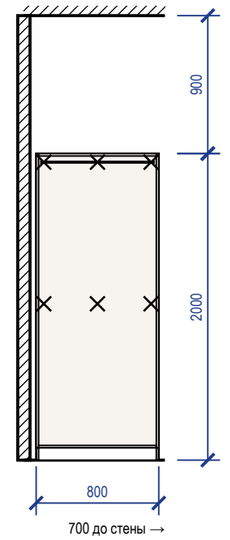


## Крепление и зазоры под отделку (изделия листа 1)

| Марка | Помещение, стена | Основание | Отделка стены | Зазор, мм | Крепёж по планке | От опрокидывания |
|---|---|---|---|---|---|---|
| M_25 | Прихожая (5), стена Б | по основанию — см. таблицу крепежа | окраска | 5 | анкер 4 шт., шаг 433 | уголки 2 шт. |
| M_30 | Спальня родителей (6), стена В | по основанию — см. таблицу крепежа | окраска | 5 | анкер 6 шт., шаг 460 | уголки 2 шт. |
| M_35 | Детская (7), стена А | по основанию — см. таблицу крепежа | окраска | 5 | анкер 4 шт., шаг 467 | уголки 2 шт. |
| M_38 | Гардеробная (8), стена А | по основанию — см. таблицу крепежа | окраска | 5 | анкер 8 шт. (2 ряда) | true |
| M_39 | Гардеробная (8), стена Г | по основанию — см. таблицу крепежа | окраска | 5 | анкер 6 шт. (2 ряда) | true |

## Крепёж по основанию стены

| Основание стены | Крепёж |
|---|---|
| бетон, ж/б | анкер-шуруп 7,5×72 или дюбель 8×60 с шурупом 5×70 |
| кирпич полнотелый | дюбель 8×80 с шурупом 5×90 |
| газобетон, пазогребень | дюбель для газобетона 10×100 или химический анкер |
| гипсокартон | закладная до обшивки (брус 40×80 или фанера 18 мм), саморез в закладную |

## Условные обозначения

- анкер / уголок крепления к стене
- корпус и полки ЛДСП (вид на стену)
- компенсатор — короб до потолка


## Примечания

1. Установочные размеры — от чистого пола и чистых стен; перед установкой контрольный замер после отделки.
2. Порядок: корпус выставить по уровню опорами цоколя → закрепить к стене по задней планке → навесить двери и фасады, отрегулировать зазоры → подогнать и закрепить компенсатор.
3. Анкеры — с шагом не более 500 мм, не ближе 50 мм от края планки; на ГКЛ только в закладную, установленную до обшивки.
4. Скрытые коммуникации под анкеры проверить детектором; трассы электрики по плану розеток.
5. Монтажная схема на 2 листах, лист 1 из 2; продолжение — на следующем листе схемы. Условные обозначения, таблица крепежа по основанию и примечания повторены на каждом листе.


| | | | | | | |
|---|---|---|---|---|---|---|
| | | | | | Проект: Дом 120 м² | |
| | Лист | № док. | Подпись | Дата | Шкафы. Монтажная схема. Лист 1 из 2 | Стадия / Лист / Листов |
| Дизайнер | Кырлан А.С. | | | 19.10.26 | | П / 9 / 104 |

выпуск 19.10.2026 № 46d0102a0d · стр. 9 из 104


**Система хранения М_40 (пом. 9)**

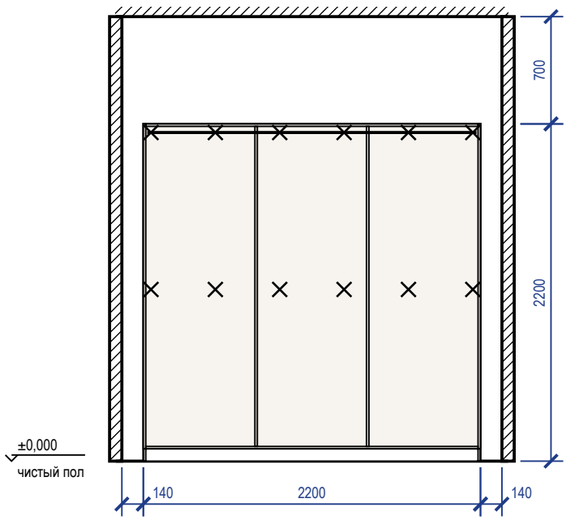



**Система хранения М_41 пом. 9**

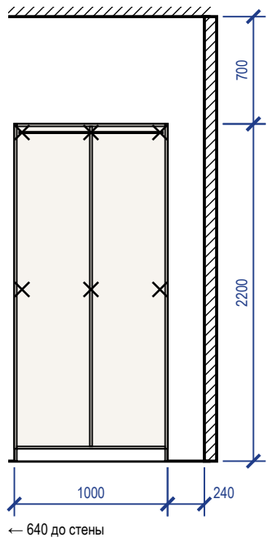


**Шкаф распашной М_45 (пом. 12)**

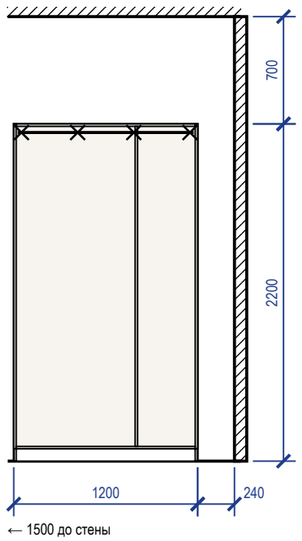


**Система хранения М_47 пом. 12**

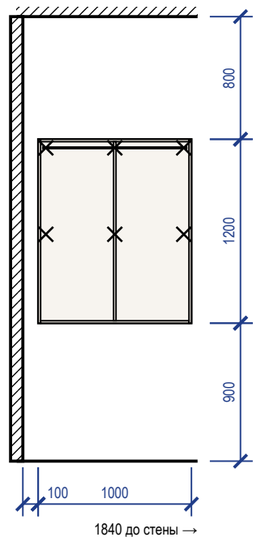


## Крепление и зазоры под отделку (изделия листа 2)

| Марка | Помещение, стена | Основание | Отделка стены | Зазор, мм | Крепёж по планке | От опрокидывания |
|---|---|---|---|---|---|---|
| М_40 | Кладовая (9), стена В | по основанию — см. таблицу крепежа | окраска | 5 | анкер 12 шт. (2 ряда) | true |
| М_41 | Кладовая (9), стена Г | по основанию — см. таблицу крепежа | окраска | 5 | анкер 6 шт. (2 ряда) | true |
| М_45 | Детская вторая (12), стена Г | по основанию — см. таблицу крепежа | окраска | 5 | анкер 4 шт., шаг 367 | уголки 2 шт. |
| М_47 | Детская вторая (12), стена Г | по основанию — см. таблицу крепежа | окраска | 5 | анкер 6 шт. (2 ряда) | true |

## Крепёж по основанию стены

| Основание стены | Крепёж |
|---|---|
| бетон, ж/б | анкер-шуруп 7,5×72 или дюбель 8×60 с шурупом 5×70 |
| кирпич полнотелый | дюбель 8×80 с шурупом 5×90 |
| газобетон, пазогребень | дюбель для газобетона 10×100 или химический анкер |
| гипсокартон | закладная до обшивки (брус 40×80 или фанера 18 мм), саморез в закладную |

## Условные обозначения


- анкер / уголок крепления к стене
- корпус и полки ЛДСП (вид на стену)
- компенсатор — короб до потолка

## Примечания

1. Установочные размеры — от чистого пола и чистых стен; перед установкой контрольный замер после отделки.
2. Порядок: корпус выставить по уровню опорами цоколя → закрепить к стене по задней планке → навесить двери и фасады, отрегулировать зазоры → подогнать и закрепить компенсатор.
3. Анкеры — с шагом не более 500 мм, не ближе 50 мм от края планки; на ГКЛ только в закладную, установленную до обшивки.
4. Скрытые коммуникации под анкеры проверить детектором; трассы электрики по плану розеток.
5. Монтажная схема на 2 листах, лист 2 из 2. Условные обозначения, таблица крепежа по основанию и примечания повторены на каждом листе.

| | | | | | | |
|---|---|---|---|---|---|---|
| | | | | | Проект: Дом 120 м² | |
| | Лист | № док. | Подпись | Дата | Шкафы. Монтажная схема. Лист 2 из 2 | Стадия / Лист / Листов |
| Дизайнер | Кырлан А.С. | | | 19.10.26 | | П / 10 / 104 |

выпуск 19.10.2026 № 46d0102a0d · стр. 10 из 104

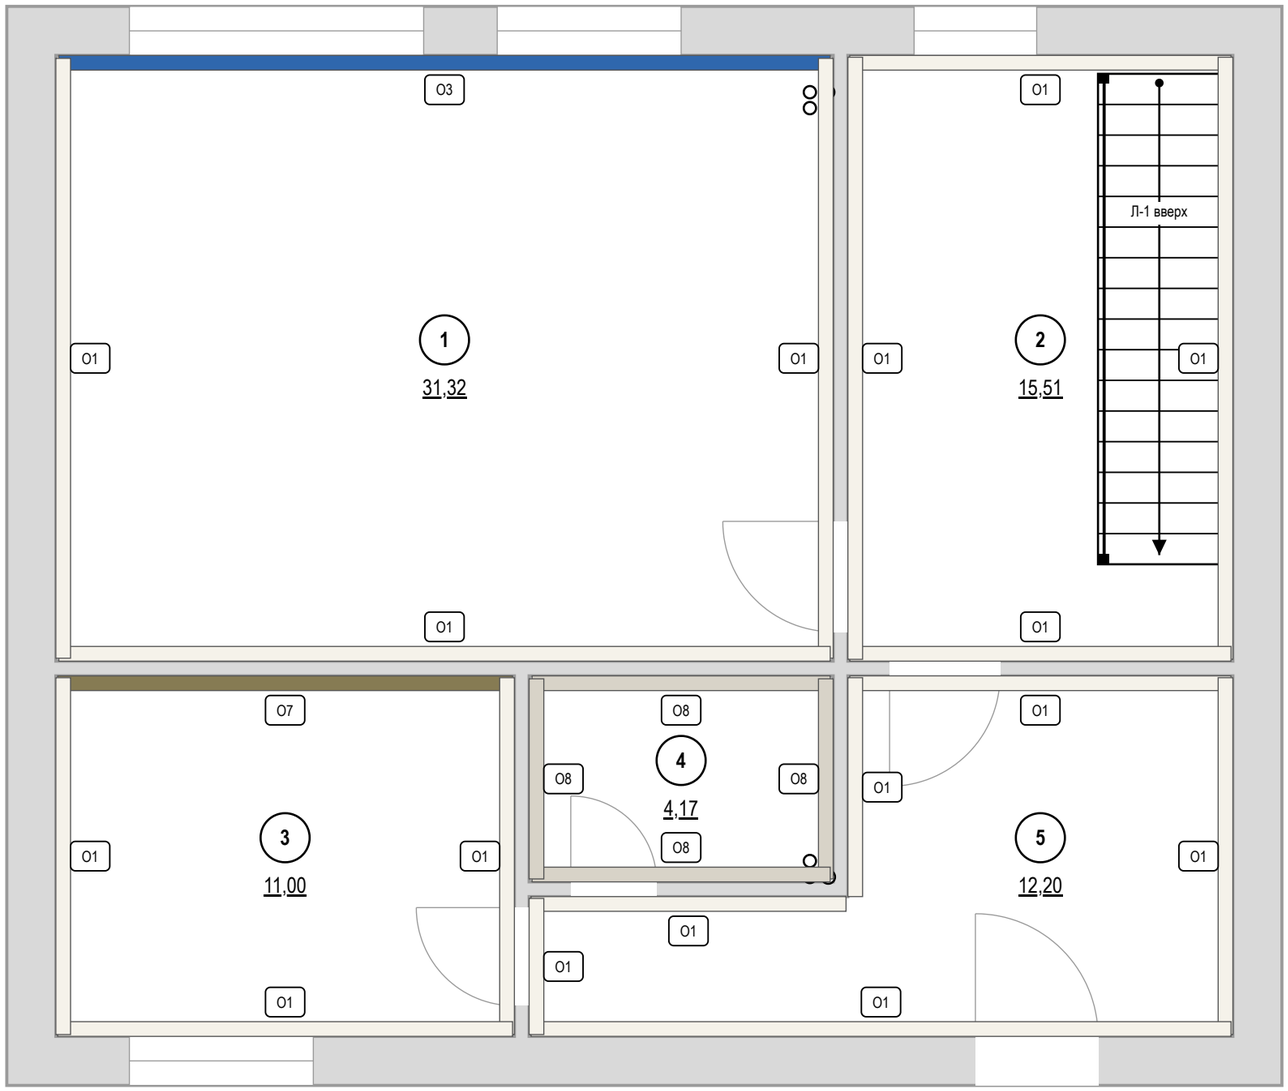


## Покрытия стен


| Марка | Покрытие | Помещение: S, м² | Итого, м² |
|---|---|---|---|
| О1 | окраска Farrow & Ball · G503 «Calla» | 1: 43,4; 2: 41,2; 3: 23,7; 5: 42,7 | 151,1 |
| О3 | окраска Farrow & Ball · S 3050-R80B «Эгейский синий» | 1: 9,8 | 9,8 |
| О7 | окраска Farrow & Ball · S 5020-G90Y «Олива» | 3: 10,8 | 10,8 |
| О8 | облицовка плиткой Atlas Concorde · A8UZ «Marvel Travertine» 600×1200 мм | 4: 18,1 | 18,1 |

Площади — нетто, по развёрткам (за вычетом проёмов и фартука); высоты помещений — от чистого пола.

| | | | | | |
|---|---|---|---|---|---|
| | | | | | Проект: Дом 120 м² |
| | Лист | № док. | Подпись | Дата | |
| Дизайнер | Кырлан А.С. | | | 19.10.26 | Карта покрытий стен · 1-й этаж |

| Стадия | Лист | Листов |
|---|---|---|
| П | 11 | 104 |

выпуск 19.10.2026 № 46d0102a0d · стр. 11 из 104

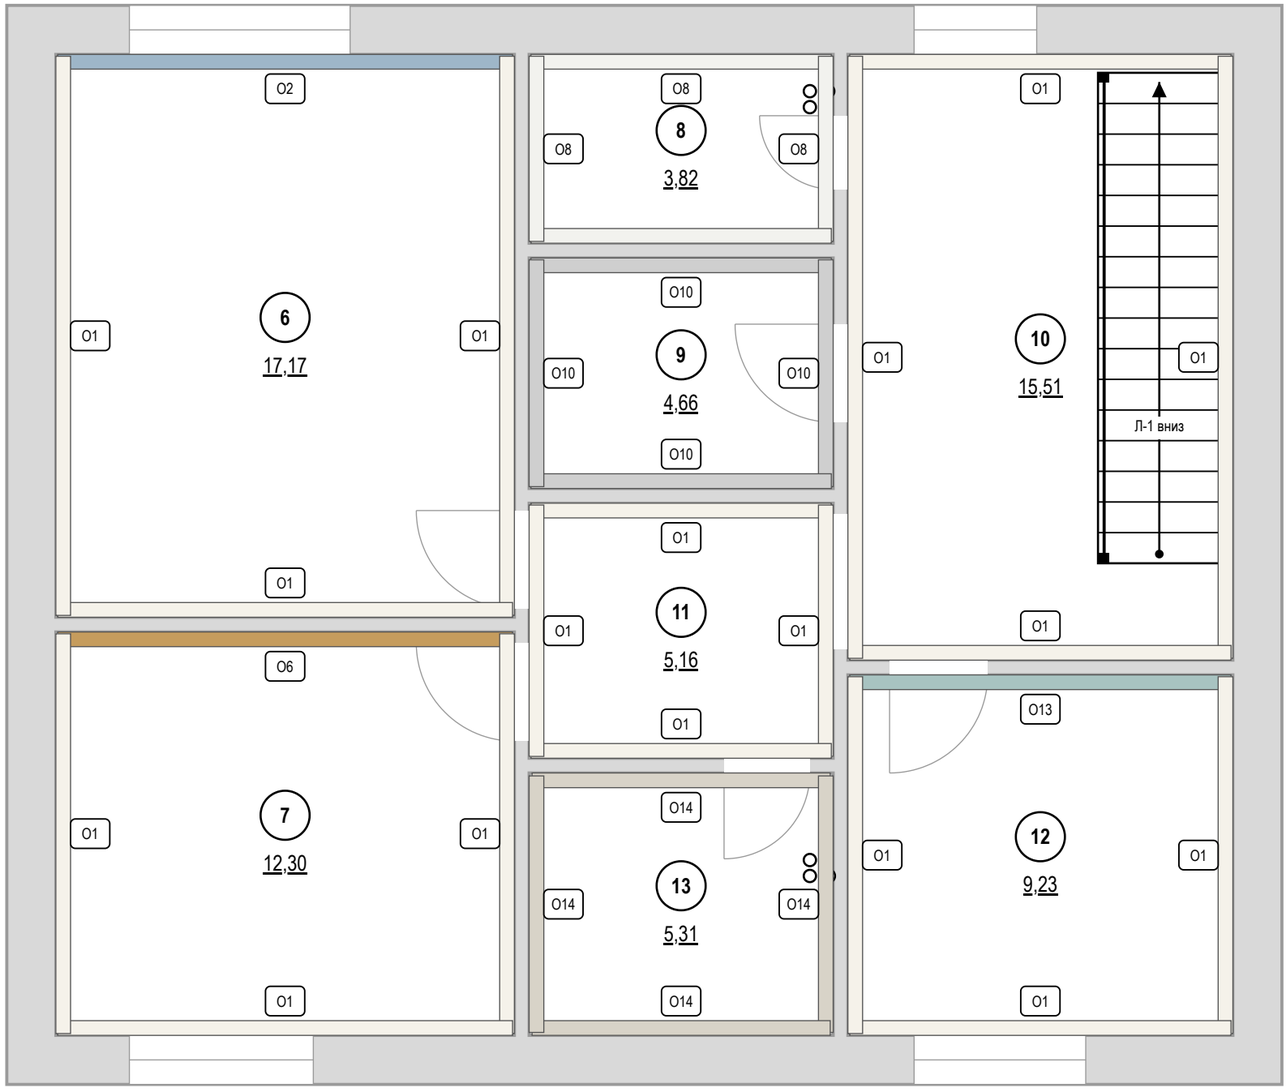


**Покрытия стен**

| Марка | Покрытие | Помещение: S, м² | Итого, м² |
|---|---|---|---|
| О1 | окраска Farrow & Ball · G503 «Calla» | 6: 35,5; 7: 25,8; 10: 38,1; 11: 19,0; 12: 23,9 | 142,3 |
| О2 | окраска Farrow & Ball · No. 89 «Lulworth Blue — светлая морская лазурь» | 6: 8,1 | 8,1 |
| О6 | окраска Farrow & Ball · No. 66 «India Yellow — охра / горчица итальянских фасадов» | 7: 10,8 | 10,8 |
| О8 | окраска Tikkurila · No. 222 «Loft White» | 8: 21,7 | 21,7 |
| О10 | окраска Tikkurila · S 0502-Y | 9: 23,3 | 23,3 |
| О13 | окраска Farrow & Ball · H440 «H440 Wave — бирюзово-голубая вода» | 12: 7,3 | 7,3 |
| О14 | облицовка плиткой Atlas Concorde · A8UZ «Marvel Travertine» 600×1200 мм | 13: 20,3 | 20,3 |

| | | | | | |
|---|---|---|---|---|---|
| | | | | | Проект: Дом 120 м² |
| | Лист | № док. | Подпись | Дата | |
| Дизайнер | Кырлан А.С. | | | 19.10.26 | Карта покрытий стен · 2-й этаж |

| Стадия | Лист | Листов |
|---|---|---|
| П | 12 | 104 |

выпуск 19.10.2026 № 46d0102a0d · стр. 12 из 104

## Колерная карта по помещениям

| Помещение | Поверхность | Образец | Поз. | Система и код цвета | Производитель, линейка / материал, артикул | Блеск | Класс EN 13300 | LRV | Площадь |
|---|---|---|---|---|---|---|---|---|---|
| **1. Гостиная-кухня** 31,32 м² | стены | | **K1** | Tikkurila G503 | Farrow & Ball · Modern Emulsion | матовая | 1 | 89 | 43,1 м² |
| | акцент А | | **K2** | NCS S 3050-R80B | Farrow & Ball · Modern Emulsion | матовая | 1 | ≈13 | 11,6 м² |
| | потолок | | **K3** | Little Greene No. 222 | Tikkurila · Anti-Reflex 2 | глубокомат. | 2 | 92 | 31,3 м² |
| | пол | | **KM1** | по образцу | Coswick · Вековые традиции | | | | 31,3 м² |
| | плинтус | | **K4** | Tikkurila G503 | МДФ · в цвет Tikkurila | | | 89 | 21,7 м |
| | фартук | | **KM2** | по образцу | керамогранит · аналог по хар. | | | | 2,0 м² |
| **2. Холл с лестницей** 15,51 м² | стены | | **K1** | Tikkurila G503 | Farrow & Ball · Modern Emulsion | матовая | 1 | 89 | 41,6 м² |
| | потолок | | **K3** | Little Greene No. 222 | Tikkurila · Anti-Reflex 2 | глубокомат. | 2 | 92 | 15,5 м² |
| | пол | | **KM1** | по образцу | Coswick · Вековые традиции | | | | 15,5 м² |
| | плинтус | | **K4** | Tikkurila G503 | МДФ · в цвет Tikkurila | | | 89 | 14,4 м |
| **3. Кабинет** 11 м² | стены | | **K1** | Tikkurila G503 | Farrow & Ball · Modern Emulsion | матовая | 1 | 89 | 24,0 м² |
| | акцент А | | **K5** | NCS S 5020-G90Y | Farrow & Ball · Modern Emulsion | матовая | 1 | ≈20 | 10,8 м² |
| | потолок | | **K3** | Little Greene No. 222 | Tikkurila · Anti-Reflex 2 | глубокомат. | 2 | 92 | 11,0 м² |
| | пол | | **KM1** | по образцу | Coswick · Вековые традиции | | | | 11,0 м² |
| | плинтус | | **K4** | Tikkurila G503 | МДФ · в цвет Tikkurila | | | 89 | 12,6 м |
| **4. Санузел гостевой** 4,17 м² | стены | | **K6** | Atlas Concorde A8UZ | Atlas Concorde · Marvel Travertine | | | | 18,5 м² |
| | потолок | | **K7** | Little Greene No. 222 | Tikkurila · Luja 7 | матовая | 1 | 92 | 4,2 м² |
| | пол | | **K6** | Atlas Concorde A8UZ | Atlas Concorde · Marvel Travertine | | | | 4,2 м² |
| **5. Прихожая** 12,2 м² | стены | | **K1** | Tikkurila G503 | Farrow & Ball · Modern Emulsion | матовая | 1 | 89 | 43,2 м² |
| | потолок | | **K3** | Little Greene No. 222 | Tikkurila · Anti-Reflex 2 | глубокомат. | 2 | 92 | 12,2 м² |
| | пол | | **K6** | Atlas Concorde A8UZ | Atlas Concorde · Marvel Travertine | | | | 12,2 м² |
| | плинтус | | **K4** | Tikkurila G503 | МДФ · в цвет Tikkurila | | | 89 | 14,0 м |


## Перечень выкрасов на согласование

| № | Код | Бренд / веер | Пом. / стена | Подложка | Формат | Статус |
|---|---|---|---|---|---|---|
| 1 | G503 | Tikkurila | 1, 2, 3, 5 | ГКЛ, загрунтованный под эту краску; МДФ, загрунтованный под эмаль | 600×1000; 300×600 | к выполнению |
| 2 | S 3050-R80B | NCS Farrow & Ball | 1 А | ГКЛ, загрунтованный под эту краску | 600×1000 | к выполнению |
| 3 | No. 222 | Little Greene | 1, 2, 3, 4, 5 | ГКЛ, загрунтованный под эту краску | 600×1000 | к выполнению |
| 4 | S 5020-G90Y | NCS Farrow & Ball | 3 А | ГКЛ, загрунтованный под эту краску | 600×1000 | к выполнению |

## Примечания

1. Цвет утверждается только по выкрасу на объекте: формат от А3 до 1000×1000 мм на загрунтованном ГКЛ, в 2 слоя (как на стене), не на белой шпаклёвке; смотреть днём и при свете проекта своего помещения, рядом с образцами пола и фасадов. Подпись на обороте: код, бренд и веер, дата.
2. Колеровка машинная в колеровочном центре бренда; каждый код — за один проход, одной партией на весь объём. Колеровщику передаётся только система и код утверждённого веера; плашки и HEX на листе — ориентир, печать не является эталоном цвета.
3. Класс мокрого истирания — EN 13300 (ISO 11998); блеск — по ГОСТ 31975 (ISO 2813), геометрия 60°. LRV — пересчёт координаты L каталога производителя (Y = ((L*+16)/116)³); «≈» — расчёт по HEX, справочно.
4. Площади поверхностей — тем же способом и с теми же цифрами, что в ведомости отделки (способ счёта — в общих указаниях); объём краски к заказу, фасовка и материалы КМ — в спецификации отделочных материалов.
5. Перечень выкрасов составлен по кодам колерной карты; к основному тону стен добавить на выкрас 2 соседних тона того же веера (светлее и темнее), статус отмечать в графе «Статус» при согласовании.

## Схема квартиры: цвет стен и акценты (б/м)

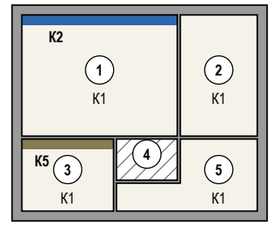


## Схема палитры проекта

Стиль: Средиземноморский 60% + Скандинавский 40% · схема: complement

| основной | основной | основной | второстепенный | второстепенный | второстепенный | акцентный | акцентный | акцентный |
|---|---|---|---|---|---|---|---|---|
| **Tikkurila G503** | **Farrow & Ball No. 239** | **Little Greene No. 222** | **NCS S 1010-Y20R** | **Farrow & Ball No. 89** | **Farrow & Ball No. 292** | **NCS S 3050-R80B** | **Farrow & Ball No. 66** | **NCS S 5020-G90Y** |
| Calla<br>LRV 89<br>стены 1,2,3,5;<br>плинтус 1,2,3,5 | Wimborne White<br>– белый с каплей тёплой охры<br>LRV ≈89<br>в отделке не применён | Loft White<br>LRV 92<br>потолок 1,2,3,4,5;<br>текстиль/декор 1,3 | Светлый песок / известняк<br>LRV 75<br>текстиль/декор 1,3 | Lulworth Blue<br>– светлая морская лазурь<br>LRV ≈45<br>в отделке не применён | Treron<br>– серо-оливковая листва<br>LRV 15<br>в отделке не применён | Эгейский синий<br>LRV ≈13<br>акцент 1;<br>текстиль/декор 1 | India Yellow<br>– охра | горчица итальянских фасадов<br>LRV 36<br>в отделке не применён | Олива<br>LRV ≈20<br>акцент 3;<br>текстиль/декор 3 |

План 60/30/10

| 60% | 30% | 10% |
|---|---|---|

Окраска, факт — по площади стен, акцентов, потолков

| 85% | 8% | 7% |
|---|---|---|

окрашено всего 267,1 м²; второстепенный тон несут мебель и текстиль

**Текстиль и декор в цветах вне палитры проекта**

Tikkurila X463 X463 Sandstone — песчаник — пом. 1 (T15, T16, T19), 3 (T9)

## Условные обозначения

- **K1** Tikkurila G503 · Calla · Modern Emulsion · матовая · кл. 1
- **K2** NCS S 3050-R80B · Эгейский синий · Farrow & Ball Modern Emulsion · матовая · кл. 1
- **K3** Little Greene No. 222 · Loft White · Anti-Reflex 2 · глубокомат. · кл. 2
- **K4** Tikkurila G503 · Calla · МДФ
- **K5** NCS S 5020-G90Y · Олива · Farrow & Ball Modern Emulsion · матовая · кл. 1
- **K6** Atlas Concorde A8UZ · Marvel Travertine · Marvel Travertine
- **K7** Little Greene No. 222 · Loft White · Luja 7 · матовая · кл. 1
- **KM1** инженерная доска · 1167-4250
- **KM2** аналог: керамогранит под травертин, матовый, 1200×600×9 мм

дерево (доска, паркет, ламинат) — рисунок досок

керамогранит, плитка, камень — сетка швов по формату

HEX не задан — цвет только по коду и вееру

К — позиция окраски (код + продукт + блеск), КМ — позиция материала, тон КМ — по описанию артикула, эталон — образец материала; ≈ LRV — расчёт по HEX, справочно

| | | | | | |
|---|---|---|---|---|---|
| | Лист | № док. | Подпись | Дата | |
| Дизайнер | Кырлан А.С. | | | 19.10.26 | Колерная карта · 1-й этаж |

Проект: Дом 120 м²

| Стадия | Лист | Листов |
|---|---|---|
| П | 13 | 104 |

выпуск 19.10.2026 № 46d0102a0d · стр. 13 из 104

## Колерная карта по помещениям

| Помещение | Поверхность | Образец | Поз. | Система и код цвета | Производитель, линейка / материал, артикул | Блеск | Класс EN 13300 | LRV | Площадь |
|---|---|---|---|---|---|---|---|---|---|
| **6. Спальня родителей** 17,17 м² | стены | | **K1** | Tikkurila G503 | Farrow & Ball · Modern Emulsion | матовая | 1 | 89 | 35,8 м² |
| | акцент А | | **K2** | Farrow & Ball No. 89 | Farrow & Ball · Modern Emulsion | матовая | 1 | ≈45 | 8,1 м² |
| | потолок | | **K3** | Little Greene No. 222 | Tikkurila · Anti-Reflex 2 | глубокомат. | 2 | 92 | 17,2 м² |
| | пол | | **KM1** | по образцу | Coswick · Вековые традиции | | | | 17,2 м² |
| | плинтус | | **K4** | Tikkurila G503 | МДФ · в цвет Tikkurila | | | 89 | 15,9 м |
| **7. Детская** 12,3 м² | стены | | **K1** | Tikkurila G503 | Farrow & Ball · Modern Emulsion | матовая | 1 | 89 | 26,1 м² |
| | акцент А | | **K5** | Farrow & Ball No. 66 | Farrow & Ball · Modern Emulsion | матовая | 1 | 36 | 10,8 м² |
| | потолок | | **K3** | Little Greene No. 222 | Tikkurila · Anti-Reflex 2 | глубокомат. | 2 | 92 | 12,3 м² |
| | пол | | **KM1** | по образцу | Coswick · Вековые традиции | | | | 12,3 м² |
| | плинтус | | **K6** | Tikkurila G503 | Orac Decor · Contour (Luxxus) | | | 89 | 13,3 м |
| **8. Гардеробная** 3,82 м² | стены | | **K7** | Little Greene No. 222 | Tikkurila · Harmony | матовая | 1 | 92 | 22,1 м² |
| | потолок | | **K3** | Little Greene No. 222 | Tikkurila · Anti-Reflex 2 | глубокомат. | 2 | 92 | 3,8 м² |
| | пол | | **KM1** | по образцу | Coswick · Вековые традиции | | | | 3,8 м² |
| | плинтус | | **K8** | Little Greene No. 222 | МДФ · в цвет Little Greene | | | 92 | 7,4 м |
| **9. Кладовая** 4,66 м² | стены | | **K9** | NCS S 0502-Y | Tikkurila | матовая | 2 | 86 | 23,6 м² |
| | потолок | | **K10** | NCS S 0300-N | Tikkurila | глубокомат. | 2 | 92 | 4,7 м² |
| | пол | | **KM1** | по образцу | Coswick · Вековые традиции | | | | 4,7 м² |
| | плинтус | | **K11** | NCS S 0300-N | Orac Decor · Contour (Luxxus) | полуматов. | | 92 | 7,9 м |
| **10. Холл второго этажа** 15,51 м² | стены | | **K1** | Tikkurila G503 | Farrow & Ball · Modern Emulsion | матовая | 1 | 89 | 38,4 м² |
| | потолок | | **K3** | Little Greene No. 222 | Tikkurila · Anti-Reflex 2 | глубокомат. | 2 | 92 | 15,5 м² |
| | пол | | **KM1** | по образцу | Coswick · Вековые традиции | | | | 15,5 м² |
| | плинтус | | **K4** | Tikkurila G503 | МДФ · в цвет Tikkurila | | | 89 | 12,9 м |
| **11. Коридор второго этажа** 5,16 м² | стены | | **K1** | Tikkurila G503 | Farrow & Ball · Modern Emulsion | матовая | 1 | 89 | 19,3 м² |
| | потолок | | **K3** | Little Greene No. 222 | Tikkurila · Anti-Reflex 2 | глубокомат. | 2 | 92 | 5,2 м² |
| | пол | | **KM1** | по образцу | Coswick · Вековые традиции | | | | 5,2 м² |
| | плинтус | | **K4** | Tikkurila G503 | МДФ · в цвет Tikkurila | | | 89 | 5,7 м |
| **12. Детская вторая** 9,23 м² | стены | | **K1** | Tikkurila G503 | Farrow & Ball · Modern Emulsion | матовая | 1 | 89 | 24,1 м² |
| | акцент А | | **K12** | Tikkurila H440 | Farrow & Ball · Modern Emulsion | матовая | 1 | ≈51 | 7,4 м² |
| | потолок | | **K3** | Little Greene No. 222 | Tikkurila · Anti-Reflex 2 | глубокомат. | 2 | 92 | 9,2 м² |
| | пол | | **KM1** | по образцу | Coswick · Вековые традиции | | | | 9,2 м² |
| | плинтус | | **K6** | Tikkurila G503 | Orac Decor · Contour (Luxxus) | | | 89 | 11,4 м |
| **13. Санузел второго этажа** 5,31 м² | стены | | **K13** | Atlas Concorde A8UZ | Atlas Concorde · Marvel Travertine | | | | 20,7 м² |
| | потолок | | **K14** | Little Greene No. 222 | Tikkurila · Luja 7 | матовая | 1 | 92 | 5,3 м² |
| | пол | | **K13** | Atlas Concorde A8UZ | Atlas Concorde · Marvel Travertine | | | | 5,3 м² |

## Примечания

1. Цвет утверждается только по выкрасу на объекте: формат от А3 до 1000×1000 мм на загрунтованном ГКЛ, в 2 слоя (как на стене), не на белой шпаклёвке; смотреть днём и при свете проекта своего помещения, рядом с образцами пола и фасадов. Подпись на обороте: код, бренд и веер, дата.
2. Колеровка машинная в колеровочном центре бренда; каждый код — за один проход, одной партией на весь объём. Колеровщику передаётся только система и код утверждённого веера; плашки и HEX на листе — ориентир, печать не является эталоном цвета.
3. Класс мокрого истирания — EN 13300 (ISO 11998); блеск — по ГОСТ 31975 (ISO 2813), геометрия 60°. LRV — пересчёт координаты L каталога производителя (Y = ((L*+16)/116)³); «≈» — расчёт по HEX, справочно.
4. Площади поверхностей — тем же способом и с теми же цифрами, что в ведомости отделки (способ счёта — в общих указаниях); объём краски к заказу, фасовка и материалы КМ — в спецификации отделочных материалов.
5. Перечень выкрасов составлен по кодам колерной карты; к основному тону стен добавить на выкрас 2 соседних тона того же веера (светлее и темнее), статус отмечать в графе «Статус» при согласовании.

## Схема палитры проекта


Стиль: Средиземноморский 60% + Скандинавский 40% · схема: complement

| основной | основной | основной | второстепенный | второстепенный | второстепенный | акцентный | акцентный | акцентный |
|---|---|---|---|---|---|---|---|---|
| **Tikkurila G503** | Farrow & Ball No. 239 | Little Greene No. 222 | NCS S 1010-Y20R | Farrow & Ball No. 89 | Farrow & Ball No. 292 | NCS S 3050-R80B | Farrow & Ball No. 66 | NCS S 5020-G90Y |
| Calla<br>LRV 89<br>стены 6,7,10,11,12; плинтус 6,7,10,11,12 | Wimborne White<br>– белый с каплей тёплой охры<br>LRV ≈89<br>в отделке не применён | Loft White<br>LRV 92<br>потолок 6,7,8,10,11,12,13; стены 8;<br>плинтус 8; текстиль/декор 6,7,12 | Светлый песок / известняк<br>LRV 75<br>текстиль/декор 6,7,12 | Lulworth Blue<br>– светлая морская лазурь<br>LRV ≈45<br>акцент 6; текстиль/декор 6 | Treron<br>– серо-оливковая листва<br>LRV 15<br>в отделке не применён | Эгейский синий<br>LRV ≈13<br>в отделке не применён | India Yellow<br>– охра / горчица итальянских фасадов<br>LRV 36<br>акцент 7; текстиль/декор 7 | Олива<br>LRV ≈20<br>в отделке не применён |

План 60/30/10




Окраска, факт — по площади стен, акцентов, потолков

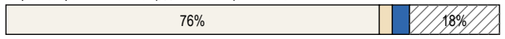


окрашено всего 309,7 м²; второстепенный тон несут мебель и текстиль

**Текстиль и декор в цветах вне палитры проекта**

- Tikkurila X395 X395 Playa — влажный пляжный песок — пом. 6 (T3)
- Tikkurila X463 X463 Sandstone — песчаник — пом. 7 (T22), 12 (T28)

## Условные обозначения

- **K1** Tikkurila G503 · Calla · Modern Emulsion · матовая · кл. 1
- **K2** Farrow & Ball No. 89 · Lulworth Blue — светлая морская лазурь · Modern Emulsion · матовая · кл. 1
- **K3** Little Greene No. 222 · Loft White · Anti-Reflex 2 · глубокомат. · кл. 2
- **K4** Tikkurila G503 · Calla · МДФ
- **K5** Farrow & Ball No. 66 · India Yellow — охра / горчица итальянских фасадов · Modern Emulsion · матовая · кл. 1
- **K6** Tikkurila G503 · Calla · Contour (Luxxus)
- **K7** Little Greene No. 222 · Loft White · Harmony · матовая · кл. 1
- **K8** Little Greene No. 222 · Loft White · МДФ
- дерево (доска, паркет, ламинат) — рисунок досок
- HEX не задан — цвет только по коду и вееру
- **K9** NCS S 0502-Y · Tikkurila · матовая · кл. 2
- **K10** NCS S 0300-N · Tikkurila · глубокомат. · кл. 2
- **K11** NCS S 0300-N · Orac Decor Contour (Luxxus) · полуматов.
- **K12** Tikkurila H440 · H440 Wave — бирюзово-голубая вода · Modern Emulsion · матовая · кл. 1
- **K13** Atlas Concorde A8UZ · Marvel Travertine · Marvel Travertine
- **K14** Little Greene No. 222 · Loft White · Luja 7 · матовая · кл. 1
- **KM1** инженерная доска · 1167-4250

К — позиция окраски (код + продукт + блеск), КМ — позиция материала, тон КМ — по описанию артикула, эталон — образец материала; ≈ LRV — расчёт по HEX, справочно

## Перечень выкрасов на согласование


| № | Код | Бренд / веер | Пом. / стена | Подложка | Формат | Статус |
|---|---|---|---|---|---|---|
| 1 | G503 | Tikkurila | 6, 7, 10, 11, 12 | ГКЛ, загрунтованный под эту краску; МДФ, загрунтованный под эмаль | 600×1000; 300×600 | к выполнению |
| 2 | No. 89 | Farrow & Ball | 6 А | ГКЛ, загрунтованный под эту краску | 600×1000 | к выполнению |
| 3 | No. 222 | Little Greene | 6, 7, 8, 10, 11, 12, 13 | ГКЛ, загрунтованный под эту краску; МДФ, загрунтованный под эмаль | 600×1000; 300×600 | к выполнению |
| | | | | | | |

… ещё 4 выкрасов — в ведомости отделки

| | | | | | |
|---|---|---|---|---|---|
| | | | | | Проект: Дом 120 м² |
| | Лист | № док. | Подпись | Дата | Колерная карта · 2-й этаж |
| Дизайнер | Кырлан А.С. | | | 19.10.26 | |

| Стадия | Лист | Листов |
|---|---|---|
| П | 14 | 104 |

выпуск 19.10.2026 № 46d0102a0d · стр. 14 из 104

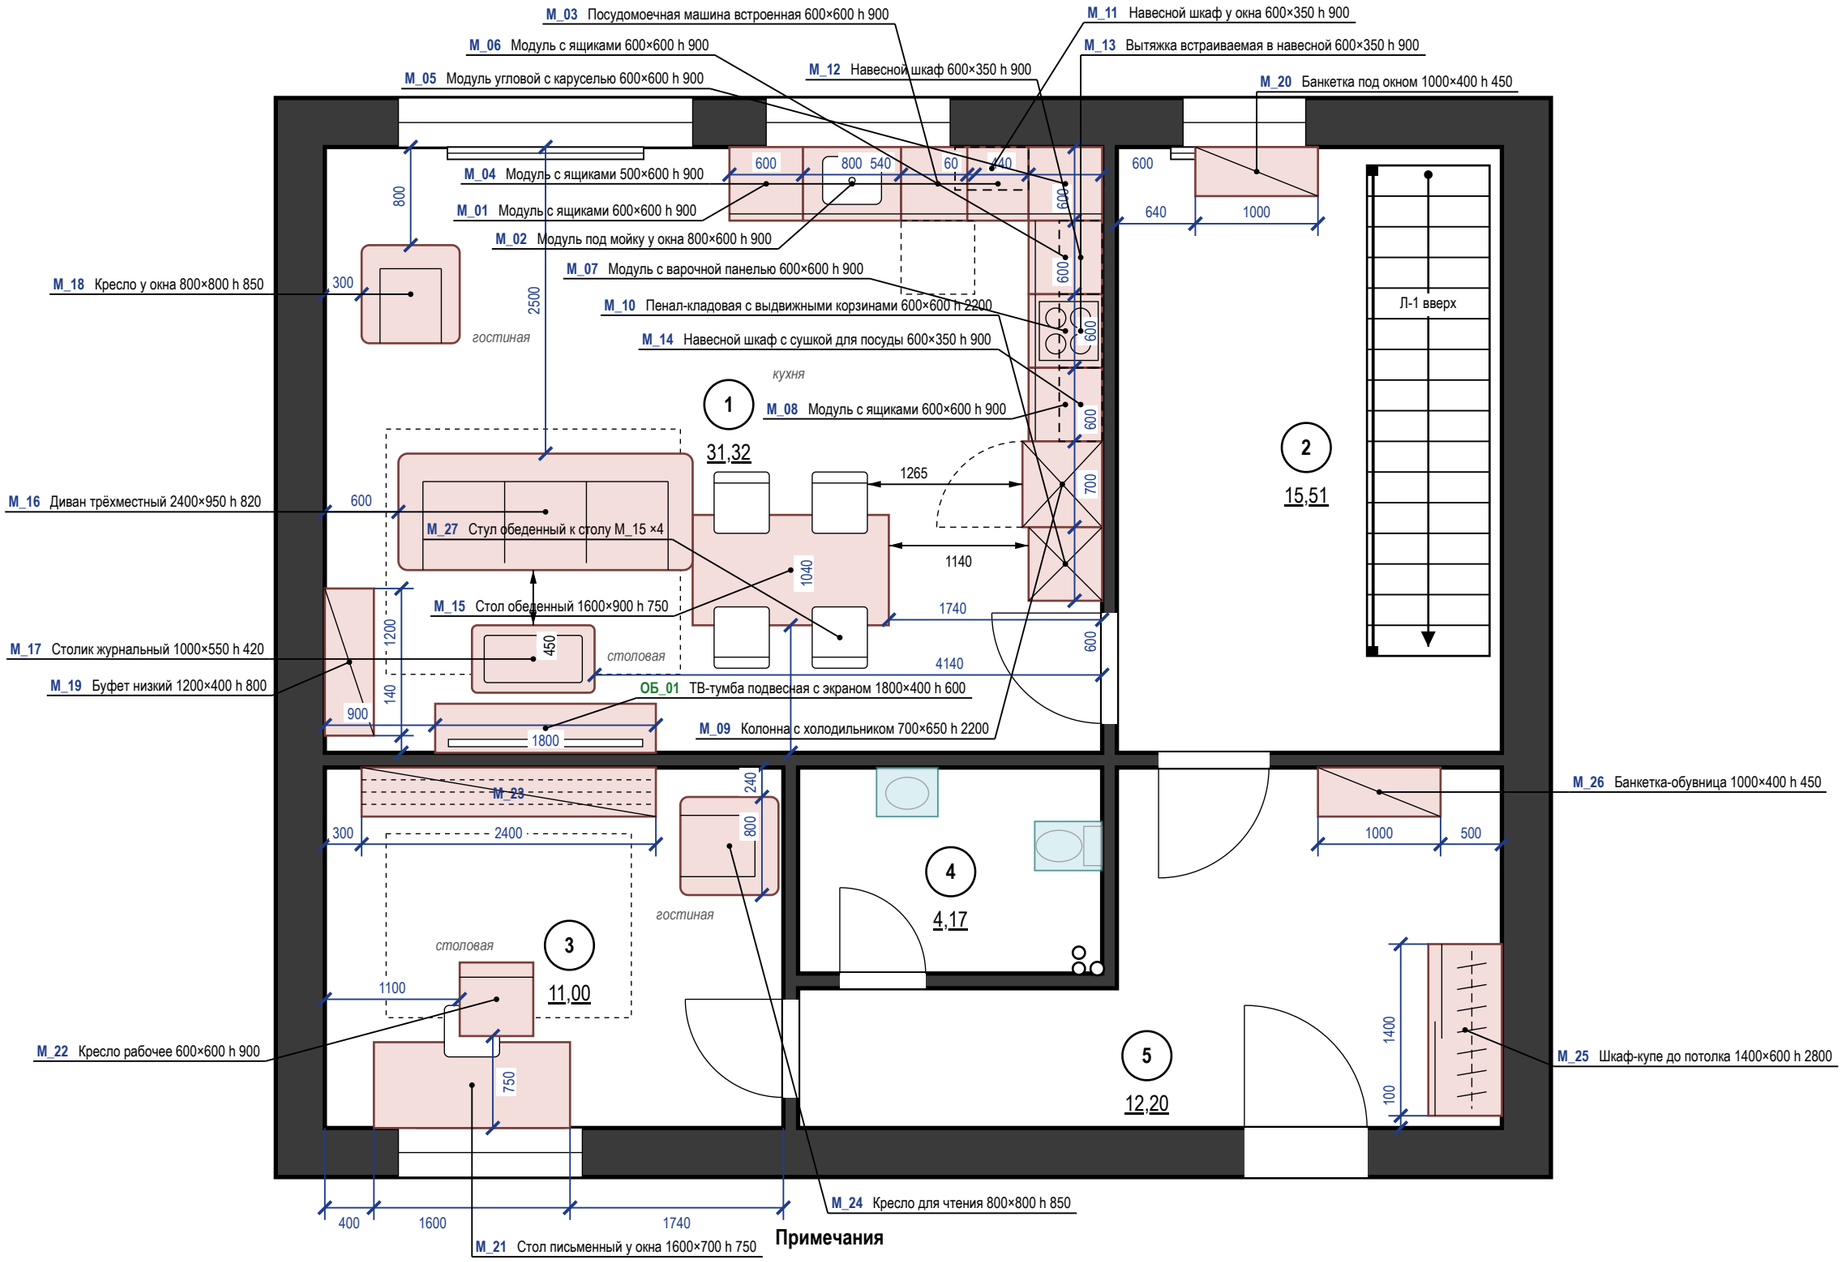


**Экспликация помещений**

лист обмерного плана · на плане — номера в марках

## Ведомость мебели и оборудования

| Марка | Наименование | Ш×Г×В, мм | Пом. | Кол. |
|---|---|---|---|---|
| M_01 | Модуль с ящиками | 600×600×900 | 1 | 1 |
| M_02 | Модуль под мойку у окна | 800×600×900 | 1 | 1 |
| M_03 | Посудомоечная машина встроенная | 600×600×900 | 1 | 1 |
| M_04 | Модуль с ящиками | 500×600×900 | 1 | 1 |
| M_05 | Модуль угловой с каруселью | 600×600×900 | 1 | 1 |
| M_06 | Модуль с ящиками | 600×600×900 | 1 | 1 |
| M_07 | Модуль с варочной панелью | 600×600×900 | 1 | 1 |
| M_08 | Модуль с ящиками | 600×600×900 | 1 | 1 |
| M_09 | Колонна с холодильником | 700×650×2200 | 1 | 1 |
| M_10 | Пенал-кладовая с выдвижными корзинами | 600×600×2200 | 1 | 1 |
| M_11 | Навесной шкаф у окна | 600×350×900 | 1 | 1 |
| M_12 | Навесной шкаф | 600×350×900 | 1 | 1 |
| M_13 | Вытяжка встраиваемая в навесной | 600×350×900 | 1 | 1 |
| M_14 | Навесной шкаф с сушкой для посуды | 600×350×900 | 1 | 1 |
| M_15 | Стол обеденный 1600×900 | 1600×900×750 | 1 | 1 |
| ОБ_01 | ТВ-тумба подвесная с экраном | 1800×400×600 | 1 | 1 |
| M_16 | Диван трёхместный | 2400×950×820 | 1 | 1 |
| M_17 | Столик журнальный | 1000×550×420 | 1 | 1 |
| M_18 | Кресло у окна | 800×800×850 | 1 | 1 |
| M_19 | Буфет низкий | 1200×400×800 | 1 | 1 |
| M_20 | Банкетка под окном | 1000×400×450 | 2 | 1 |
| M_21 | Стол письменный у окна | 1600×700×750 | 3 | 1 |
| M_22 | Кресло рабочее | 600×600×900 | 3 | 1 |
| M_23 | Стеллаж для книг во всю стену | 2400×400×2400 | 3 | 1 |
| M_24 | Кресло для чтения | 800×800×850 | 3 | 1 |
| M_25 | Шкаф-купе до потолка | 1400×600×2800 | 5 | 1 |
| M_26 | Банкетка-обувница | 1000×400×450 | 5 | 1 |
| M_27 | Стул обеденный к столу M_15 | 450×500×820 | 1 | 4 |

Ш — вдоль стены (изголовья), Г — от стены (длина кровати)

Материалы, модели, допуск замены — лист 17


## Примечания

1. Размеры — в мм от чистовых поверхностей стен; размеры мебели уточнить после отделочных работ; общие указания — лист 2.
2. Отступ от стены, на плане не образмерен: M_24 — 40 мм.
3. Стулья обеденной группы (M_27 — 4 шт.) показаны в рабочем положении, задвинутыми под столешницу на 150 мм.

| | | | | | |
|---|---|---|---|---|---|
| | | | | | Проект: Дом 120 м² |
| | Лист | № док. | Подпись | Дата | План размещения мебели и оборудования · 1-й этаж |
| Дизайнер | Кырлан А.С. | | | 19.10.26 | |

| Стадия | Лист | Листов |
|---|---|---|
| П | 15 | 104 |

выпуск 19.10.2026 № 46d0102a0d · стр. 15 из 104

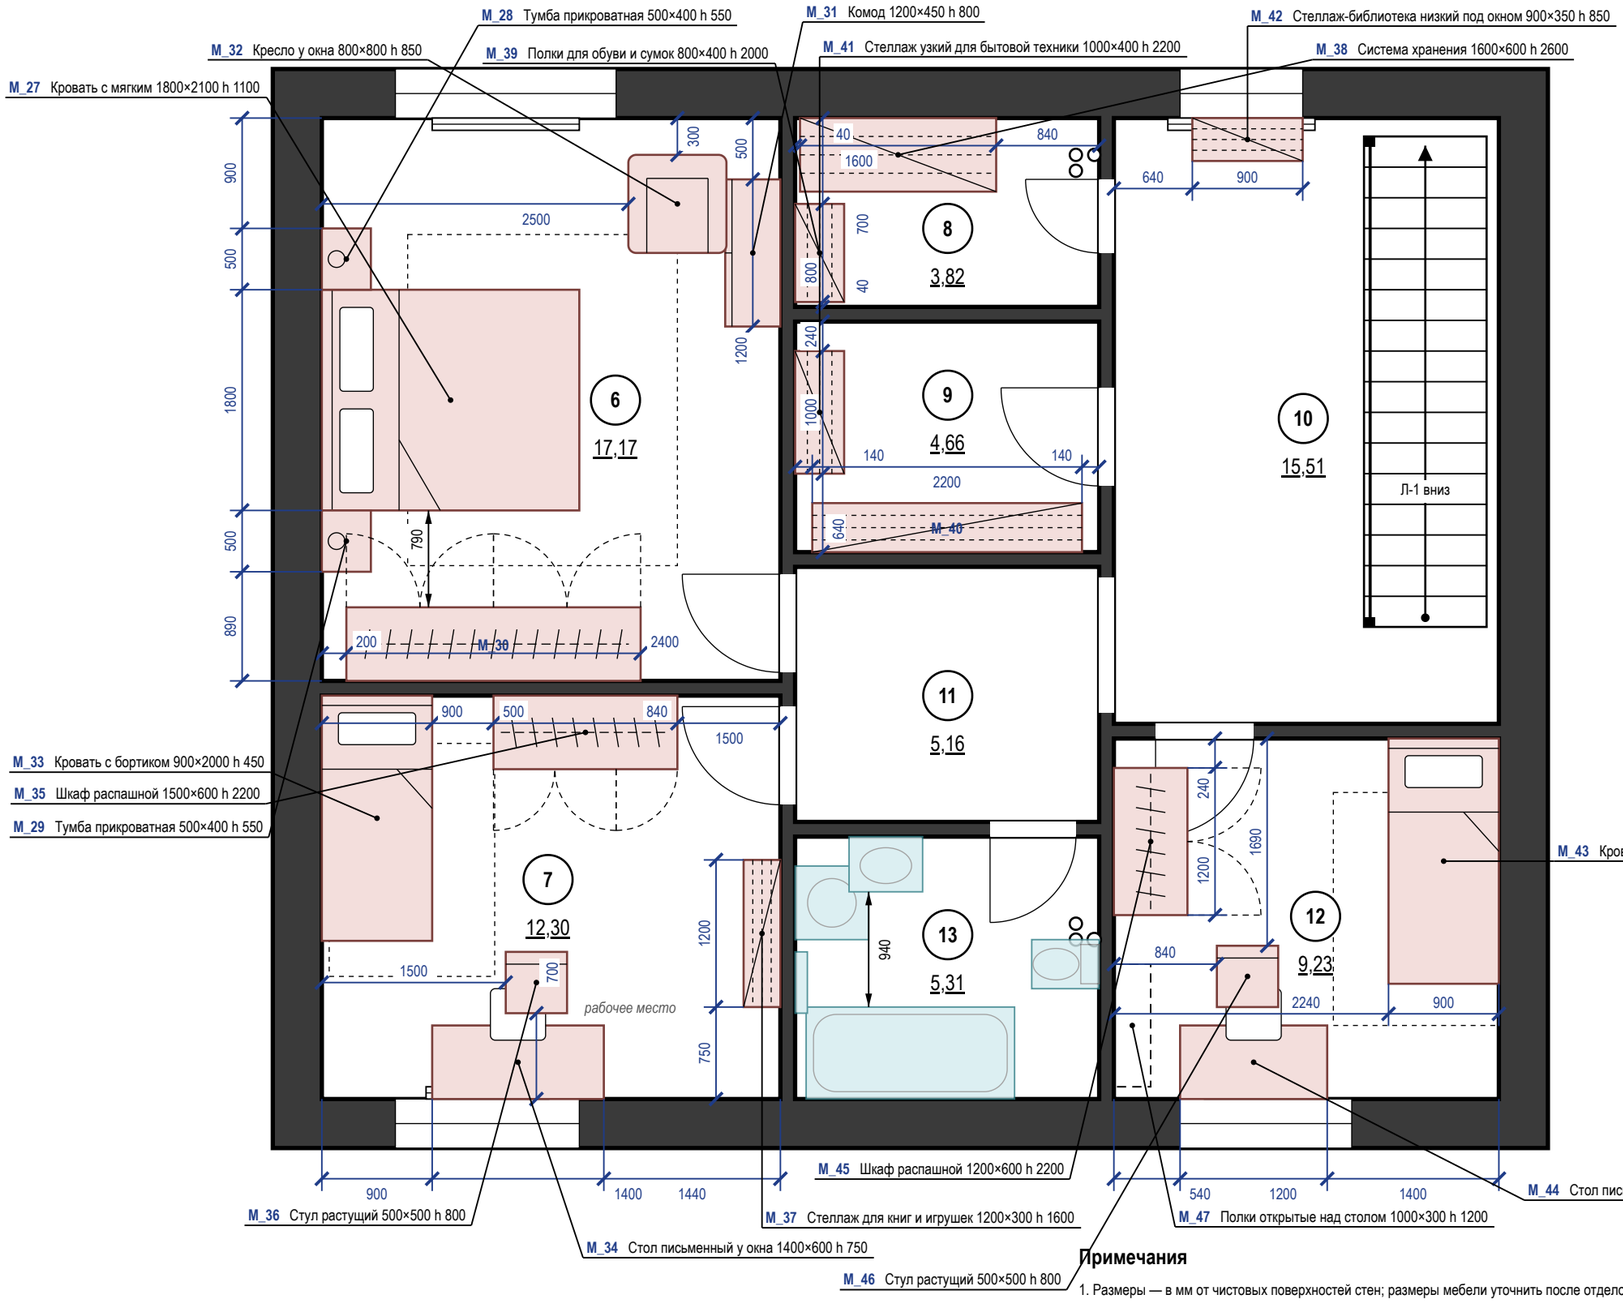


**Экспликация помещений**

лист обмерного плана · на плане — номера в марках

## Ведомость мебели и оборудования

| Марка | Наименование | Ш×Г×В, мм | Пом. | Кол. |
|---|---|---|---|---|
| M_27 | Кровать 1800×2000 с мягким | 1800×2100×1100 | 6 | 1 |
| M_28 | Тумба прикроватная | 500×400×550 | 6 | 1 |
| M_29 | Тумба прикроватная | 500×400×550 | 6 | 1 |
| M_30 | Шкаф распашной до потолка | 2400×600×2600 | 6 | 1 |
| M_31 | Комод | 1200×450×800 | 6 | 1 |
| M_32 | Кресло у окна | 800×800×850 | 6 | 1 |
| M_33 | Кровать 900×2000 с бортиком | 900×2000×450 | 7 | 1 |
| M_34 | Стол письменный у окна | 1400×600×750 | 7 | 1 |
| M_35 | Шкаф распашной | 1500×600×2200 | 7 | 1 |
| M_36 | Стул растущий | 500×500×800 | 7 | 1 |
| M_37 | Стеллаж для книг и игрушек | 1200×300×1600 | 7 | 1 |
| M_38 | Система хранения | 1600×600×2600 | 8 | 1 |
| M_39 | Полки для обуви и сумок | 800×400×2000 | 8 | 1 |
| M_40 | Стеллаж для хранения | 2200×400×2200 | 9 | 1 |
| M_41 | Стеллаж узкий для бытовой техники | 1000×400×2200 | 9 | 1 |
| M_42 | Стеллаж-библиотека низкий под окном | 900×350×850 | 10 | 1 |
| M_43 | Кровать 900×2000 с бортиком | 900×2000×450 | 12 | 1 |
| M_44 | Стол письменный у окна | 1200×600×750 | 12 | 1 |
| M_45 | Шкаф распашной | 1200×600×2200 | 12 | 1 |
| M_46 | Стул растущий | 500×500×800 | 12 | 1 |
| M_47 | Полки открытые над столом | 1000×300×1200 | 12 | 1 |

Ш — вдоль стены (изголовья), Г — от стены (длина кровати)

Материалы, модели, допуск замены — лист 17

**Примечания**

1. Размеры — в мм от чистовых поверхностей стен; размеры мебели уточнить после отделочных работ; общие указания — лист 2.

| | | | | | |
|---|---|---|---|---|---|
| | | | | | Проект: Дом 120 м² |
| | Лист | № док. | Подпись | Дата | План размещения мебели и оборудования · 2-й этаж |
| Дизайнер | Кырлан А.С. | | | 19.10.26 | |

| Стадия | Лист | Листов |
|---|---|---|
| П | 16 | 104 |

выпуск 19.10.2026 № 46d0102a0d · стр. 16 из 104

| Поз. | Наименование и техническая характеристика | Тип, марка, обозначение документа, опросного листа | Код продукции | Поставщик | Ед. измерения | Кол. | Масса 1 ед., кг | Примечание |
|---|---|---|---|---|---|---|---|---|
| | **Мебель встроенная и корпусная (изготовление по чертежам мебельщика)** | | | | | | | |
| M_01 | Модуль с ящиками; корпус ЛДСП, фасады — матовая эмаль в тон стен; Ш×Г×В 600×600×900 мм | | | изготовление на заказ | шт. | 1 | | пом. 1 |
| M_02 | Модуль под мойку у окна; корпус ЛДСП, фасады — матовая эмаль в тон стен; Ш×Г×В 800×600×900 мм | | | изготовление на заказ | шт. | 1 | | пом. 1 |
| M_03 | Посудомоечная машина встроенная; корпус ЛДСП, фасады — матовая эмаль в тон стен; Ш×Г×В 600×600×900 мм | | | изготовление на заказ | шт. | 1 | | пом. 1 |
| M_04 | Модуль с ящиками; корпус ЛДСП, фасады — матовая эмаль в тон стен; Ш×Г×В 500×600×900 мм | | | изготовление на заказ | шт. | 1 | | пом. 1 |
| M_05 | Модуль угловой с каруселью; корпус ЛДСП, фасады — матовая эмаль в тон стен; Ш×Г×В 600×600×900 мм | | | изготовление на заказ | шт. | 1 | | пом. 1 |
| M_06 | Модуль с ящиками; корпус ЛДСП, фасады — матовая эмаль в тон стен; Ш×Г×В 600×600×900 мм | | | изготовление на заказ | шт. | 1 | | пом. 1 |
| M_07 | Модуль с варочной панелью и духовым шкафом; корпус ЛДСП, фасады — матовая эмаль в тон стен; Ш×Г×В 600×600×900 мм | | | изготовление на заказ | шт. | 1 | | пом. 1 |
| M_08 | Модуль с ящиками; корпус ЛДСП, фасады — матовая эмаль в тон стен; Ш×Г×В 600×600×900 мм | | | изготовление на заказ | шт. | 1 | | пом. 1 |
| M_09 | Колонна с холодильником; корпус ЛДСП, фасады — матовая эмаль в тон стен; Ш×Г×В 700×650×2200 мм | | | изготовление на заказ | шт. | 1 | | пом. 1 |
| M_10 | Пенал-кладовая с выдвижными корзинами; корпус ЛДСП, фасады — матовая эмаль в тон стен; Ш×Г×В 600×600×2200 мм | | | изготовление на заказ | шт. | 1 | | пом. 1 |
| M_11 | Навесной шкаф у окна, витрина со стеклом; корпус ЛДСП, фасады — матовая эмаль в тон стен; Ш×Г×В 600×350×900 мм | | | изготовление на заказ | шт. | 1 | | пом. 1 |
| M_12 | Навесной шкаф, фасад в тон цоколя; корпус ЛДСП, фасады — матовая эмаль в тон стен; Ш×Г×В 600×350×900 мм | | | изготовление на заказ | шт. | 1 | | пом. 1 |
| M_13 | Вытяжка встраиваемая в навесной шкаф; корпус ЛДСП, фасады — матовая эмаль в тон стен; Ш×Г×В 600×350×900 мм | | | изготовление на заказ | шт. | 1 | | пом. 1 |
| M_14 | Навесной шкаф с сушкой для посуды; корпус ЛДСП, фасады — матовая эмаль в тон стен; Ш×Г×В 600×350×900 мм | | | изготовление на заказ | шт. | 1 | | пом. 1 |
| M_25 | Шкаф-купе до потолка, дуб табак; корпус ЛДСП, фасады — матовая эмаль в цвет стен (Tikkurila G503); Ш×Г×В 1400×600×2800 мм | | | изготовление на заказ | шт. | 1 | | пом. 5 |
| M_30 | Шкаф распашной до потолка, фасады матовые; корпус ЛДСП, фасады — матовая эмаль в цвет стен (Tikkurila G503); Ш×Г×В 2400×600×2600 мм | | | изготовление на заказ | шт. | 1 | | пом. 6 |
| M_35 | Шкаф распашной; корпус ЛДСП, фасады — матовая эмаль в цвет стен (Tikkurila G503); Ш×Г×В 1500×600×2200 мм | | | изготовление на заказ | шт. | 1 | | пом. 7 |
| M_38 | Система хранения: штанги, полки, ящики; каркас и полки — ЛДСП, декор «дуб натуральный»; Ш×Г×В 1600×600×2600 мм | | | изготовление на заказ | шт. | 1 | | пом. 8; крепление к стене |
| M_39 | Полки для обуви и сумок; каркас и полки — ЛДСП, декор «дуб натуральный»; Ш×Г×В 800×400×2000 мм | | | изготовление на заказ | шт. | 1 | | пом. 8; крепление к стене |
| M_45 | Шкаф распашной; корпус ЛДСП, фасады — матовая эмаль в цвет стен (Tikkurila G503); Ш×Г×В 1200×600×2200 мм | | | изготовление на заказ | шт. | 1 | | пом. 12 |
| | **Мебель покупная** | | | | | | | |
| M_15 | Стол обеденный 1600×900, дуб табак; шпон, дуб натуральный, матовое масло; Ш×Г×В 1600×900×750 мм | | | аналог по характеристикам | шт. | 1 | | пом. 1; замена ≤ габарита |
| M_16 | Диван трёхместный, лён; обивка — ткань, цвет NCS S 1010-Y20R; Ш×Г×В 2400×950×820 мм | | | аналог по характеристикам | шт. | 1 | | пом. 1; замена ≤ габарита |
| M_17 | Столик журнальный, дуб и латунь; шпон, дуб натуральный, матовое масло; Ш×Г×В 1000×550×420 мм | | | аналог по характеристикам | шт. | 1 | | пом. 1; замена ≤ габарита |
| M_18 | Кресло у окна, букле; обивка — ткань, цвет NCS S 1010-Y20R; Ш×Г×В 800×800×850 мм | | | аналог по характеристикам | шт. | 1 | | пом. 1; замена ≤ габарита |
| M_19 | Буфет низкий, дуб табак; шпон, дуб натуральный, матовое масло; Ш×Г×В 1200×400×800 мм | | | аналог по характеристикам | шт. | 1 | | пом. 1; крепление к стене; замена ≤ габарита |
| M_48 | Стул обеденный к столу M_15; обивка — ткань, цвет NCS S 1010-Y20R; каркас — дуб натуральный; Ш×Г×В 450×500×820 мм | | | аналог по характеристикам | шт. | 4 | | пом. 1; замена ≤ габарита |
| ОБ_01 | ТВ-тумба подвесная с экраном, дуб табак; шпон, дуб натуральный, матовое масло; Ш×Г×В 1800×400×600 мм | | | аналог по характеристикам | шт. | 1 | | пом. 1; замена ≤ габарита |
| M_20 | Банкетка под окном, дуб табак; Ш×Г×В 1000×400×450 мм | | | аналог по характеристикам | шт. | 1 | | пом. 2; замена ≤ габарита |
| M_21 | Стол письменный у окна, дуб табак; шпон, дуб натуральный, матовое масло; Ш×Г×В 1600×700×750 мм | | | аналог по характеристикам | шт. | 1 | | пом. 3; замена ≤ габарита |
| M_22 | Кресло рабочее; обивка — ткань, цвет NCS S 1010-Y20R; каркас — дуб натуральный; Ш×Г×В 600×600×900 мм | | | аналог по характеристикам | шт. | 1 | | пом. 3; замена ≤ габарита |
| M_23 | Стеллаж для книг во всю стену; шпон, дуб натуральный, матовое масло; Ш×Г×В 2400×400×2400 мм | | | аналог по характеристикам | шт. | 1 | | пом. 3; крепление к стене; замена ≤ габарита |
| M_24 | Кресло для чтения; обивка — ткань, цвет NCS S 1010-Y20R; Ш×Г×В 800×800×850 мм | | | аналог по характеристикам | шт. | 1 | | пом. 3; замена ≤ габарита |
| M_26 | Банкетка-обувница; Ш×Г×В 1000×400×450 мм | | | аналог по характеристикам | шт. | 1 | | пом. 5; замена ≤ габарита |
| M_27 | Кровать 1800×2000 с мягким изголовьем 1100, лён; мягкое изголовье, обивка — ткань, цвет NCS S 1010-Y20R; Ш×Г×В 1800×2100×1100 мм | | | аналог по характеристикам | шт. | 1 | | пом. 6; замена ≤ габарита |

## Примечания

1. Позиции мебели совпадают с марками на плане расстановки; размеры Ш×Г×В — Ш вдоль стены, Г от стены.
2. Встроенная и корпусная мебель изготавливается по чертежам мебельщика после контрольного обмера; графы «Тип, марка» и «Код продукции» для неё не заполняются (ГОСТ 21.110-2013).
3. Покупные изделия — аналог по характеристикам: заменять только на изделия не больше указанного габарита и того же материала и цвета.
4. Материал и цвет, не указанные в данных изделия, приняты по концепции: тон дерева — по полу, обивка — по вторичному цвету палитры; образцы согласовать до заказа.
5. Масса 1 ед. для изделий до 25 кг не указывается. Техника — по монтажным схемам изготовителя; выводы — по листам ЭОМ и ВК.

| | | | | | |
|---|---|---|---|---|---|
| | | | | | Проект: Дом 120 м² |
| | Лист | № док. | Подпись | Дата | Спецификация мебели и оборудования |
| Дизайнер | Кырлан А.С. | | | 19.10.26 | |

| Стадия | Лист | Листов |
|---|---|---|
| П | 17 | 104 |

| Поз. | Наименование и техническая характеристика | Тип, марка, обозначение документа, опросного листа | Код продукции | Поставщик | Ед. измерения | Кол. | Масса 1 ед., кг | Примечание |
|---|---|---|---|---|---|---|---|---|
| M_28, M_29 | Тумба прикроватная, дуб табак; шпон, дуб натуральный, матовое масло; Ш×Г×В 500×400×550 мм | | | аналог по характеристикам | шт. | 2 | | пом. 6; замена ≤ габарита |
| M_31 | Комод, дуб табак; шпон, дуб натуральный, матовое масло; Ш×Г×В 1200×450×800 мм | | | аналог по характеристикам | шт. | 1 | | пом. 6; крепление к стене; замена ≤ габарита |
| M_32 | Кресло у окна; обивка — ткань, цвет NCS S 1010-Y20R; Ш×Г×В 800×800×850 мм | | | аналог по характеристикам | шт. | 1 | | пом. 6; замена ≤ габарита |
| M_33, M_43 | Кровать 900×2000 с бортиком; мягкое изголовье, обивка — ткань, цвет NCS S 1010-Y20R; Ш×Г×В 900×2000×450 мм | | | аналог по характеристикам | шт. | 2 | | пом. 7, 12; замена ≤ габарита |
| M_34 | Стол письменный у окна; шпон, дуб натуральный, матовое масло; Ш×Г×В 1400×600×750 мм | | | аналог по характеристикам | шт. | 1 | | пом. 7; замена ≤ габарита |
| M_36, M_46 | Стул растущий; обивка — ткань, цвет NCS S 1010-Y20R; каркас — дуб натуральный; Ш×Г×В 500×500×800 мм | | | аналог по характеристикам | шт. | 2 | | пом. 7, 12; замена ≤ габарита |
| M_37 | Стеллаж для книг и игрушек; шпон, дуб натуральный, матовое масло; Ш×Г×В 1200×300×1600 мм | | | аналог по характеристикам | шт. | 1 | | пом. 7; крепление к стене; замена ≤ габарита |
| M_40 | Стеллаж для хранения; каркас и полки — ЛДСП, декор «дуб натуральный»; Ш×Г×В 2200×400×2200 мм | | | аналог по характеристикам | шт. | 1 | | пом. 9; крепление к стене; замена ≤ габарита |
| M_41 | Стеллаж узкий для бытовой техники; каркас и полки — ЛДСП, декор «дуб натуральный»; Ш×Г×В 1000×400×2200 мм | | | аналог по характеристикам | шт. | 1 | | пом. 9; крепление к стене; замена ≤ габарита |
| M_42 | Стеллаж-библиотека низкий под окном; шпон, дуб натуральный, матовое масло; Ш×Г×В 900×350×850 мм | | | аналог по характеристикам | шт. | 1 | | пом. 10; крепление к стене; замена ≤ габарита |
| M_44 | Стол письменный у окна; шпон, дуб натуральный, матовое масло; Ш×Г×В 1200×600×750 мм | | | аналог по характеристикам | шт. | 1 | | пом. 12; замена ≤ габарита |
| M_47 | Полки открытые над столом; каркас и полки — ЛДСП, декор «дуб натуральный»; Ш×Г×В 1000×300×1200 мм | | | аналог по характеристикам | шт. | 1 | | пом. 12; крепление к стене; замена ≤ габарита |
| | **Техника встраиваемая и бытовая, светильники под розетки** | | | | | | | |
| | Посудомоечная машина встраиваемая, в модуле M_03; ниша 600 мм | | | аналог по характеристикам | шт. | 1 | | пом. 1; по схеме изготовителя |
| | Варочная панель встраиваемая, электрическая, в модуле M_07 | | | аналог по характеристикам | шт. | 1 | | пом. 1; по схеме изготовителя |
| | Духовой шкаф встраиваемый, в модуле M_07 | | | аналог по характеристикам | шт. | 1 | | пом. 1; по схеме изготовителя |
| | Холодильник встраиваемый, в модуле M_09 | | | аналог по характеристикам | шт. | 1 | | пом. 1; по схеме изготовителя |
| | Вытяжка встраиваемая, в модуле M_13 | | | аналог по характеристикам | шт. | 1 | | пом. 1; по схеме изготовителя |
| | Стиральная машина, место по листу ВК (ОБ_02); Ш×Г 600×600 мм | | | аналог по характеристикам | шт. | 1 | | пом. 13; по схеме изготовителя |
| | Торшер, у поз. M_18; абажур — ткань или опаловое стекло; лампа 2700 K | | | аналог по характеристикам | шт. | 1 | | пом. 1; розетка Р21 (ЭОМ) |
| | Торшер, у поз. M_32; абажур — ткань или опаловое стекло; лампа 2700 K | | | аналог по характеристикам | шт. | 1 | | пом. 6; розетка Р5 (ЭОМ) |
| | **Текстиль** | | | | | | | |
| T13 | Портьеры-волна (гостиная); лён 70 %, вискоза 30 %; цвет NCS S 1010-Y20R; карниз 3000 мм, высота 2870 мм, сборка 2 | | | аналог по характеристикам | шт. | 2 | | пом. 1 |
| T14 | Тюль (гостиная); полиэстер 100 %; цвет Little Greene No. 222; карниз 3000 мм, высота 2870 мм, сборка 2,5 | | | аналог по характеристикам | шт. | 1 | | пом. 1 |
| T15 | Римская штора (кухня); лён 100 %; цвет Tikkurila X463; карниз 1500 мм, высота 1600 мм | | | аналог по характеристикам | шт. | 1 | | пом. 1 |
| T16 | Ковёр в зоне отдыха; шерсть 100 %; цвет Tikkurila X463; 2400×2000 мм | | | аналог по характеристикам | шт. | 1 | | пом. 1; с подложкой |
| T17 | Подушки на диван; букле (шерсть 60 %, полиэстер 40 %); цвет NCS S 1010-Y20R | | | аналог по характеристикам | шт. | 3 | | пом. 1 |
| T18 | Подушки на диван, акцент; хлопковый бархат 100 %; цвет NCS S 3050-R80B | | | аналог по характеристикам | шт. | 2 | | пом. 1 |
| T19 | Плед на диван; альпака 50 %, шерсть 50 %; цвет Tikkurila X463 | | | аналог по характеристикам | шт. | 1 | | пом. 1 |
| T7 | Портьеры-волна; лён 100 %; цвет NCS S 1010-Y20R; карниз 2100 мм, высота 2870 мм, сборка 2 | | | аналог по характеристикам | шт. | 2 | | пом. 3 |
| T8 | Тюль; полиэстер 100 %; цвет Little Greene No. 222; карниз 2100 мм, высота 2870 мм, сборка 2,5 | | | аналог по характеристикам | шт. | 1 | | пом. 3 |
| T9 | Ковёр под кроватью; шерсть 100 %; цвет Tikkurila X463; 2000×1500 мм | | | аналог по характеристикам | шт. | 1 | | пом. 3; с подложкой |
| T10 | Подушки декоративные на кровать; букле (шерсть 60 %, полиэстер 40 %); цвет NCS S 1010-Y20R | | | аналог по характеристикам | шт. | 3 | | пом. 3 |
| T11 | Подушки на кровать, акцент; хлопковый бархат 100 %; цвет NCS S 5020-G90Y | | | аналог по характеристикам | шт. | 2 | | пом. 3 |
| T12 | Плед на кровать; шерсть мериноса 100 %; цвет NCS S 5020-G90Y | | | аналог по характеристикам | шт. | 1 | | пом. 3 |

| | Лист | № док. | Подпись | Дата |
|---|---|---|---|---|
| Дизайнер | Кырлан А.С. | | | 19.10.26 |

Проект: Дом 120 м²

Спецификация мебели и оборудования (продолжение)

| Стадия | Лист | Листов |
|---|---|---|
| П | 18 | 104 |

выпуск 19.10.2026 № 46d0102a0d · стр. 18 из 104

| Поз. | Наименование и техническая характеристика | Тип, марка, обозначение документа, опросного листа | Код продукции | Поставщик | Ед. измерения | Кол. | Масса 1 ед., кг | Примечание |
|---|---|---|---|---|---|---|---|---|
| Т1 | Портьеры-волна; лён 100 %; цвет NCS S 1010-Y20R; карниз 2400 мм, высота 2870 мм, сборка 2 | | | аналог по характеристикам | шт. | 2 | | пом. 6 |
| Т2 | Тюль; полиэстер 100 %; цвет Little Greene No. 222; карниз 2400 мм, высота 2870 мм, сборка 2,5 | | | аналог по характеристикам | шт. | 1 | | пом. 6 |
| Т3 | Ковёр под кроватью; шерсть 80 %, хлопок 20 %; цвет Tikkurila X395; 2200×2700 мм | | | аналог по характеристикам | шт. | 1 | | пом. 6; с подложкой |
| Т4 | Подушки декоративные на кровать; лён 100 %; цвет NCS S 1010-Y20R | | | аналог по характеристикам | шт. | 3 | | пом. 6 |
| Т5 | Подушки на кровать, акцент; хлопковый бархат 100 %; цвет Farrow & Ball No. 89 | | | аналог по характеристикам | шт. | 2 | | пом. 6 |
| Т6 | Плед на кровать; шерсть мериноса 100 %; цвет Farrow & Ball No. 89 | | | аналог по характеристикам | шт. | 1 | | пом. 6 |
| Т20 | Портьеры-волна; лён 100 %; цвет NCS S 1010-Y20R; карниз 2100 мм, высота 2870 мм, сборка 2 | | | аналог по характеристикам | шт. | 2 | | пом. 7 |
| Т21 | Тюль; полиэстер 100 %; цвет Little Greene No. 222; карниз 2100 мм, высота 2870 мм, сборка 2,5 | | | аналог по характеристикам | шт. | 1 | | пом. 7 |
| Т22 | Ковёр под кроватью; шерсть 100 %; цвет Tikkurila X463; 1350×1900 мм | | | аналог по характеристикам | шт. | 1 | | пом. 7; с подложкой |
| Т23 | Подушки декоративные на кровать; букле (шерсть 60 %, полиэстер 40 %); цвет NCS S 1010-Y20R | | | аналог по характеристикам | шт. | 3 | | пом. 7 |
| Т24 | Подушки на кровать, акцент; хлопковый бархат 100 %; цвет Farrow & Ball No. 66 | | | аналог по характеристикам | шт. | 2 | | пом. 7 |
| Т25 | Плед на кровать; шерсть мериноса 100 %; цвет Farrow & Ball No. 66 | | | аналог по характеристикам | шт. | 1 | | пом. 7 |
| Т26 | Портьеры-волна; лён 100 %; цвет NCS S 1010-Y20R; карниз 2000 мм, высота 2870 мм, сборка 2 | | | аналог по характеристикам | шт. | 2 | | пом. 12 |
| Т27 | Тюль; полиэстер 100 %; цвет Little Greene No. 222; карниз 2000 мм, высота 2870 мм, сборка 2,5 | | | аналог по характеристикам | шт. | 1 | | пом. 12 |
| Т28 | Ковёр под кроватью; шерсть 100 %; цвет Tikkurila X463; 1350×1900 мм | | | аналог по характеристикам | шт. | 1 | | пом. 12; с подложкой |
| Т29 | Подушки декоративные на кровать; букле (шерсть 60 %, полиэстер 40 %); цвет NCS S 1010-Y20R | | | аналог по характеристикам | шт. | 3 | | пом. 12 |
| Т30 | Подушки на кровать, акцент; хлопковый бархат 100 %; цвет Tikkurila H440 | | | аналог по характеристикам | шт. | 2 | | пом. 12 |
| Т31 | Плед на кровать; шерсть мериноса 100 %; цвет Tikkurila H440 | | | аналог по характеристикам | шт. | 1 | | пом. 12 |
| | **Декор** | | | | | | | |
| ДК6 | Картина над креслом: пейзаж, масло, рама — дуб табак; 1000×800 мм; центр на 1550 мм от пола | | | аналог по характеристикам | шт. | 1 | 6 | пом. 1; крепление: анкер, 2 шт. |
| ДК7 | Растение в кашпо; 450×450 мм | | | аналог по характеристикам | шт. | 1 | | пом. 1 |
| ДК8 | Ваза керамическая с ветками на обеденном столе; 200×350 мм; на M_15 | | | аналог по характеристикам | шт. | 1 | | пом. 1 |
| ДК40 | Олива в кадке Ø450 у окна; 450×450 мм | | | аналог по характеристикам | шт. | 1 | | пом. 1 |
| ДК41 | Сансевиерия в кашпо Ø400 под лестницей; 400×400 мм | | | аналог по характеристикам | шт. | 1 | | пом. 2 |
| ДК3 | Картина над креслом: гравюра в паспарту, рама — графит; 550×450 мм; низ на 1050 мм от пола | | | аналог по характеристикам | шт. | 1 | 4 | пом. 3; крепление к стене |
| ДК9 | Зеркало над умывальником, влагостойкое; 500×700 мм; низ на 1100 мм от пола | | | аналог по характеристикам | шт. | 1 | 4 | пом. 4; крепление к стене |
| ДК5 | Зеркало; рама — чёрный матовый; 600×1800 мм; низ на 550 мм от пола | | | аналог по характеристикам | шт. | 1 | 18 | пом. 5; крепление: анкер, 4 шт. |
| ДК43 | Замиокулькас в кашпо Ø350; 350×350 мм | | | аналог по характеристикам | шт. | 1 | | пом. 5 |
| ДК1 | Картина над кроватью: акварель, рама — светлый дуб; 1000×700 мм; низ на 1300 мм от пола | | | аналог по характеристикам | шт. | 1 | 4 | пом. 6; крепление к стене |
| ДК44 | Аглаонема в кашпо Ø400; 400×400 мм | | | аналог по характеристикам | шт. | 1 | | пом. 6 |
| ДК2 | Картина над кроватью: детская иллюстрация, рама — белёный дуб; 600×450 мм; низ на 650 мм от пола | | | аналог по характеристикам | шт. | 1 | 4 | пом. 7; крепление к стене |
| ДК4 | Зеркало в рост в тонкой чёрной раме; рама — чёрный матовый; 500×1600 мм; низ на 300 мм от пола | | | аналог по характеристикам | шт. | 1 | 12 | пом. 7; крепление: анкер для пустотелых оснований, 4 шт. |
| ДК45 | Хлорофитум в кашпо Ø350 у окна; 350×350 мм | | | аналог по характеристикам | шт. | 1 | | пом. 10 |
| ДК46 | Сансевиерия в кашпо Ø400; 400×400 мм | | | аналог по характеристикам | шт. | 1 | | пом. 11 |
| ДК10 | Картина над кроватью: детский принт, рама — светлый ясень; 600×450 мм; низ на 650 мм от пола | | | аналог по характеристикам | шт. | 1 | 4 | пом. 12; крепление к стене |
| ДК11 | Зеркало в рост в тонкой чёрной раме; рама — чёрный матовый; 500×1600 мм; низ на 300 мм от пола | | | аналог по характеристикам | шт. | 1 | 12 | пом. 12; крепление: анкер для пустотелых оснований, 4 шт. |
| ДК12 | Зеркало над умывальником, влагостойкое; 600×750 мм; низ на 1100 мм от пола | | | аналог по характеристикам | шт. | 1 | 4 | пом. 13; крепление к стене |

| | Лист | № док. | Подпись | Дата |
|---|---|---|---|---|
| Дизайнер | Кырлан А.С. | | | 19.10.26 |

Проект: Дом 120 м²

Спецификация мебели и оборудования (продолжение)

| Стадия | Лист | Листов |
|---|---|---|
| П | 19 | 104 |

выпуск 19.10.2026 № 46d0102a0d · стр. 19 из 104

## Ведомость изделий

| Марка | Наименование | Пом. | Ш×Г×В, мм | Корпус | Фасад | Кромка, мм скр./вид. | Кол. |
|---|---|---|---|---|---|---|---|
| M_25 | Шкаф-купе | 5 | 1400×600×2800 | ЛДСП 16 | рифлёные панели МДФ в алюминиевом профиле | 0,4 / 2 | 1 |
| M_30 | Шкаф распашной | 6 | 2400×600×2600 | ЛДСП 16 | МДФ 18, эмаль матовая | 0,4 / 2 | 1 |
| M_35 | Шкаф распашной | 7 | 1500×600×2200 | ЛДСП 16 | МДФ 18, эмаль матовая | 0,4 / 2 | 1 |
| M_38 | Система хранения | 8 | 1600×600×2600 | ЛДСП 16 | без фасадов; ящики — МДФ 18, эмаль матовая | 0,4 / 2 | 1 |
| M_39 | Система хранения | 8 | 800×400×2000 | ЛДСП 16 | без фасадов; ящики — МДФ 18, эмаль матовая | 0,4 / 2 | 1 |
| M_40 | Система хранения | 9 | 2200×400×2200 | ЛДСП 16 | без фасадов; ящики — МДФ 18, эмаль матовая | 0,4 / 2 | 1 |
| M_41 | Система хранения | 9 | 1000×400×2200 | ЛДСП 16 | без фасадов; ящики — МДФ 18, эмаль матовая | 0,4 / 2 | 1 |
| M_45 | Шкаф распашной | 12 | 1200×600×2200 | ЛДСП 16 | МДФ 18, эмаль матовая | 0,4 / 2 | 1 |
| M_47 | Система хранения | 12 | 1000×300×1200 | ЛДСП 16 | без фасадов; ящики — МДФ 18, эмаль матовая | 0,4 / 2 | 1 |
| M_01 | Модуль нижний: ящики | 1 | 600×600×900 | ЛДСП 16 | МДФ 18, эмаль матовая | 0,4 / 2 | 1 |
| M_02 | Модуль нижний: мойка | 1 | 800×600×900 | ЛДСП 16 | МДФ 18, эмаль матовая | 0,4 / 2 | 1 |
| M_03 | Модуль нижний: ПММ | 1 | 600×600×900 | ЛДСП 16 | МДФ 18, эмаль матовая | 0,4 / 2 | 1 |
| M_11 | Модуль навесной: полки | 1 | 600×350×900 | ЛДСП 16 | МДФ 18, эмаль матовая | 0,4 / 2 | 1 |
| M_04 | Модуль нижний: ящики | 1 | 500×600×900 | ЛДСП 16 | МДФ 18, эмаль матовая | 0,4 / 2 | 1 |
| M_05 | Модуль нижний: ящики | 1 | 600×600×900 | ЛДСП 16 | МДФ 18, эмаль матовая | 0,4 / 2 | 1 |
| M_06 | Модуль нижний: ящики | 1 | 600×600×900 | ЛДСП 16 | МДФ 18, эмаль матовая | 0,4 / 2 | 1 |
| M_12 | Модуль навесной: полки | 1 | 600×350×900 | ЛДСП 16 | МДФ 18, эмаль матовая | 0,4 / 2 | 1 |
| M_07 | Модуль нижний: духовой шкаф, варочная | 1 | 600×600×900 | ЛДСП 16 | МДФ 18, эмаль матовая | 0,4 / 2 | 1 |
| M_13 | Модуль навесной: полки | 1 | 600×350×900 | ЛДСП 16 | МДФ 18, эмаль матовая | 0,4 / 2 | 1 |
| M_08 | Модуль нижний: ящики | 1 | 600×600×900 | ЛДСП 16 | МДФ 18, эмаль матовая | 0,4 / 2 | 1 |
| M_14 | Модуль навесной: полки | 1 | 600×350×900 | ЛДСП 16 | МДФ 18, эмаль матовая | 0,4 / 2 | 1 |
| M_09 | Пенал: холодильник встр. | 1 | 700×650×2200 | ЛДСП 16 | МДФ 18, эмаль матовая | 0,4 / 2 | 1 |
| M_10 | Пенал: полки | 1 | 600×600×2200 | ЛДСП 16 | МДФ 18, эмаль матовая | 0,4 / 2 | 1 |

## Ведомость встраиваемой техники

| Поз. | Прибор | Ниша, вырез, мм | Вентиляция | Питание | Схема |
|---|---|---|---|---|---|
| M_02 | Мойка врезная / подстольная с сифоном | вырез по шаблону, ориентир 700 × 480 | | смеситель — выводы ВК | по модели |
| M_03 | Посудомоечная машина встраиваемая, 60 см | ниша 600 × 862 (от пола до низа столешницы) | зазор в цоколе, по схеме | розетка в соседнем модуле | по модели |
| M_07 | Духовой шкаф встраиваемый, 60 см | ниша 560 × 595, глубина ≥ 550 | зазор за шкафом, вырез в задней стенке | вывод кабеля под шкафом | по модели |
| M_07 | Варочная панель индукционная, 60 см | вырез в столешнице 560 × 490 | | вывод кабеля под модулем | по модели |
| M_09 | Холодильник встраиваемый, ниша 1780 | ниша 1780 × 560 × 550 | решётка в цоколе, канал за корпусом, выход сверху | розетка над нишей или в соседнем модуле | по модели |
| M_07 | Вытяжка настенная, 60 см | низ ≥ 650 над панелью | воздуховод к вентканалу, короб до потолка | вывод кабеля в коробе | по модели |

## Ведомость фурнитуры

| № | Фурнитура | Тип, размер | Изделия | Кол. |
|---|---|---|---|---|
| 1 | Система дверей купе: профиль, направляющие, ролики | на 2 двери | M_25 | 1 |
| 2 | Ручка-профиль вертикальная | в цвет профиля | M_25 | 2 |
| 3 | Полкодержатель с фиксацией | ø5 мм | M_25, M_30, M_35, M_38, M_40, M_41, M_45, M_47, M_11, M_12, M_13, M_14, M_09, M_10 | 256 |
| 4 | Штанга овальная 30×15, L = 676 | + 2 держателя | M_25 | 1 |
| 5 | Полка для обуви выдвижная наклонная | ширина 676 | M_25 | 3 |
| 6 | Опора регулируемая с цоколем на клипсах | ход 20 мм | M_25, M_30, M_35, M_38, M_39, M_40, M_41, M_45 | 50 |
| 7 | Анкер по основанию стены | по таблице крепежа | M_25, M_30, M_35, M_38, M_39, M_40, M_41, M_45, M_47, M_11, M_12, M_13, M_14 | 64 |
| 8 | Уголок крепления к стене от опрокидывания | стальной | M_25, M_30, M_35, M_38, M_39, M_40, M_41, M_45, M_47, M_09, M_10 | 22 |
| 9 | Петля накладная 110° с доводчиком | чашка 35 мм | M_30, M_35, M_45, M_02, M_11, M_12, M_13, M_14, M_09, M_10 | 98 |
| 10 | Штанга овальная 30×15, L = 936 | + 2 держателя | M_30 | 2 |
| 11 | Штанга овальная 30×15, L = 456 | + 2 держателя | M_30 | 1 |
| 12 | Штанга овальная 30×15, L = 976 | + 2 держателя | M_35 | 1 |
| 13 | Штанга овальная 30×15, L = 776 | + 2 держателя | M_38, M_45 | 2 |
| 14 | Штанга выдвижная торцевая | L по глубине | M_39, M_40, M_41 | 5 |
| 15 | Направляющие полного выдвижения с доводчиком NL 500 | пара | M_01, M_04, M_05, M_06, M_07, M_08 | 16 |
| 16 | Ручка-профиль | латунь матовая | M_01, M_02, M_03, M_11, M_04, M_05, M_06, M_12, M_07, M_13, M_08, M_14, M_09, M_10 | 32 |
| 17 | Опора кухонная регулируемая 100–120 мм | + клипса цоколя | M_01, M_02, M_03, M_04, M_05, M_06, M_07, M_08, M_09, M_10 | 44 |
| 18 | Комплект навески фасада ПММ | из поставки машины | M_03 | 1 |
| 19 | Навес регулируемый для навесного шкафа | пара на секцию | M_11, M_12, M_13, M_14 | 4 |
| 20 | Шина монтажная | L = 540 | M_11, M_12, M_13, M_14 | 4 |


## Примечания

1. Модели техники выбирает заказчик до изготовления мебели; ниши, вырезы и вентиляция — по монтажной схеме выбранной модели (условие гарантии), её номер вносится в ведомость.
2. Количество фурнитуры — по чертежам изделий; запас крепежа 5 %. Аналоги — по характеристикам (доводчик, нагрузка, ход).
3. Цвет корпусов, фасадов и профилей — по колерной карте проекта.


| | | | | | Проект: Дом 120 м² | | | |
|---|---|---|---|---|---|---|---|---|
| | Лист | № док. | Подпись | Дата | Ведомости изделий, техники и фурнитуры | Стадия | Лист | Листов |
| Дизайнер | Кырлан А.С. | | | 19.10.26 | | П | 20 | 104 |

выпуск 19.10.2026 № 46d0102a0d · стр. 20 из 104

## Фрагмент 1. Санузел гостевой (пом. 4)

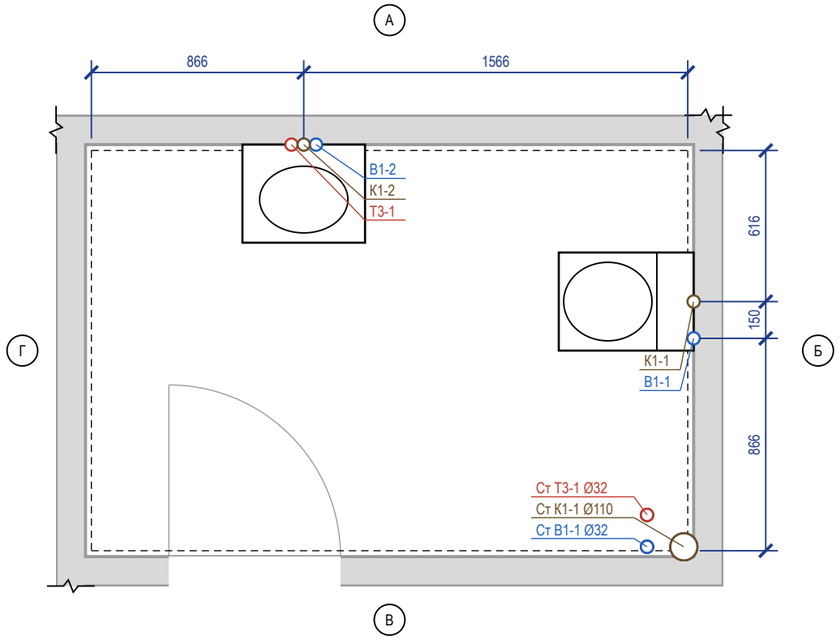


## Фрагмент 2. Гостиная-кухня (пом. 1)

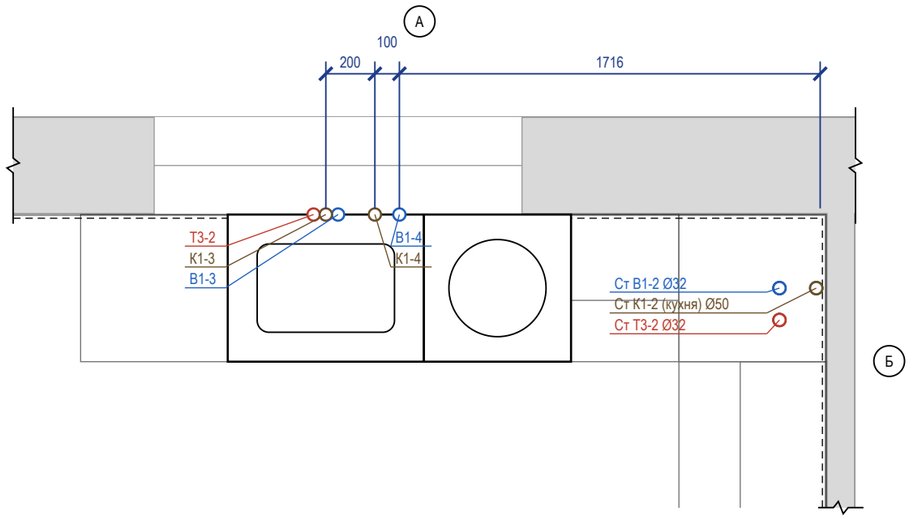


## Ведомость привязок выводов

| Код | Прибор | Ø | H, мм | Привязка от чист. стен, мм | Прим. |
|---|---|---|---|---|---|
| В1-1 | С_01 унитаз подвесной | ½" | 250 | ст. Б: 766 от А | в раме инсталляции |
| К1-1 | С_01 унитаз подвесной | Ø110 | 220 | ст. Б: 616 от А | |
| В1-2 | С_02 умывальник | ½" | 600 | ст. А: 916 от Г | межос. 100 |
| Т3-1 | С_02 умывальник | ½" | 600 | ст. А: 816 от Г | межос. 100 |
| К1-2 | С_02 умывальник | Ø50 | 500 | ст. А: 866 от Г | |
| В1-3 | П3 мойка кухонная | ½" | 600 | ст. А: 1966 от Б | межос. 100 |
| Т3-2 | П3 мойка кухонная | ½" | 600 | ст. А: 2066 от Б | межос. 100 |
| К1-3 | П3 мойка кухонная | Ø50 | 400 | ст. А: 2016 от Б | |
| В1-4 | П4 посудомоечная машина | ½" | 550 | ст. А: 1716 от Б | кран ПММ в шкафу мойки |
| К1-4 | П4 посудомоечная машина | Ø40 | 550 | ст. А: 1816 от Б | слив ПММ в шкафу мойки |

## Условные обозначения

- вывод В1 (код — в ведомости привязок)
- вывод Т3 (код — в ведомости привязок)
- вывод К1 (код — в ведомости привязок)
- сантехприбор по расстановке (габарит модели)
- чистовая поверхность стены (от неё привязки)
- стояк «Ст К1-N / Ст В1-N» (ГОСТ 21.601), Ø мм
- линия обрыва (граница фрагмента)
- А — обозначение стены А–Г (как на развёртках)

## Примечания


1. Привязки выводов даны от чистовых поверхностей стен (облицовка на сторону: санузел гостевой — 24 мм (штукатурка 10 + клей 5 + плитка 9); гостиная-кухня — 24 мм (фартук: штукатурка 10 + клей 5 + плитка 9)); эти же грани — на развёртках и в раскладке плитки. Высоты — от чистого пола помещения.
2. До черновой разводки сверить по паспорту выбранного прибора (смеситель, инсталляция, сифон).
3. Горячая вода (Т3) — слева от холодной (В1), если смотреть на прибор. Допуск установки выводов: ±5 мм в группе, ±20 мм у отдельно стоящих.
4. Расчёт систем водоснабжения и канализации и подбор оборудования выполняет проектная организация; лист задаёт места и высоты выводов.
5. Посудомоечная машина П4: кран и слив — отдельными выводами в шкафу мойки (не за машиной), до машины ≤ 1500 мм.
6. Прибор П3 мойка кухонная, П4 посудомоечная машина взят из расстановки мебели (по шкафу с мойкой).
7. Стояки в коробах/шахтах не замоноличивать; стояк К1 в коробе — звукоизоляция стояка в коробе без жёсткого контакта с трубой; к арматуре и ревизиям — люк не меньше 300×400.

| | | | | | |
|---|---|---|---|---|---|
| | | | | | Проект: Дом 120 м² |
| | Лист | № док. | Подпись | Дата | План выводов сантехники · 1-й этаж |
| Дизайнер | Кырлан А.С. | | | 19.10.26 | |

| Стадия | Лист | Листов |
|---|---|---|
| П | 21 | 104 |

выпуск 19.10.2026 № 46d0102a0d · стр. 21 из 104

## Фрагмент 1. Санузел второго этажа (пом. 13)

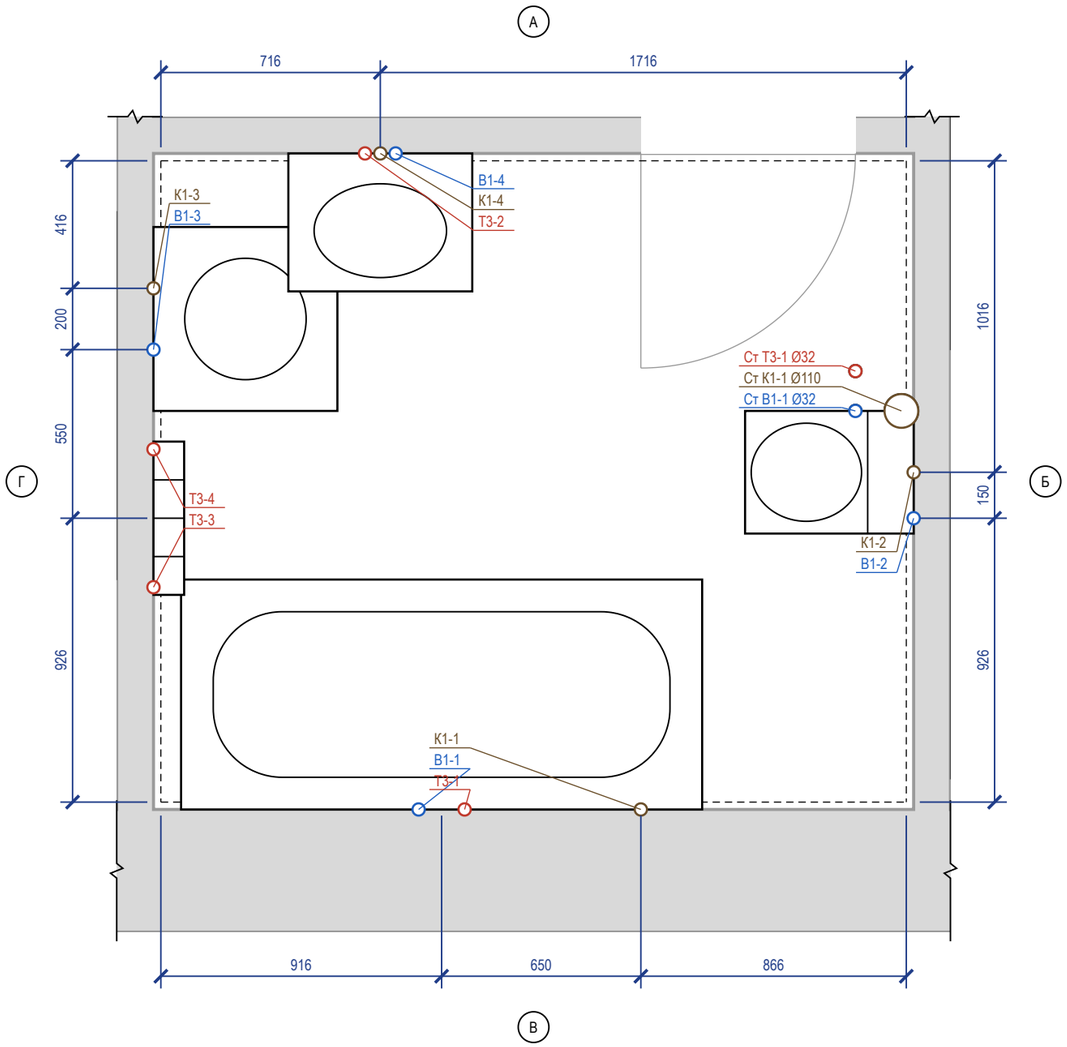


## Ведомость привязок выводов

| Код | Прибор | Ø | H, мм | Привязка от чист. стен, мм | Прим. |
|---|---|---|---|---|---|
| В1-1 | С_03 ванна | ½" | 800 | ст. В: 841 от Г | межос. 150 |
| Т3-1 | С_03 ванна | ½" | 800 | ст. В: 991 от Г | межос. 150 |
| К1-1 | С_03 ванна | Ø50 | 50 | ст. В: 866 от Б | |
| В1-2 | С_04 унитаз подвесной | ½" | 250 | ст. Б: 926 от В | в раме инсталляции |
| К1-2 | С_04 унитаз подвесной | Ø110 | 220 | ст. Б: 1016 от А | |
| В1-3 | ОБ_02 стиральная машина | ½" | 600 | ст. Г: 616 от А | кран машины |
| К1-3 | ОБ_02 стиральная машина | Ø50 | 600 | ст. Г: 416 от А | |
| В1-4 | С_05 умывальник | ½" | 600 | ст. А: 766 от Г | межос. 100 |
| Т3-2 | С_05 умывальник | ½" | 600 | ст. А: 666 от Г | межос. 100 |
| К1-4 | С_05 умывальник | Ø50 | 500 | ст. А: 716 от Г | |
| Т3-3 | С_06 полотенцесушитель | ½" | 1150 | ст. Г: 701 от В | подача, межос. 450; байпас и краны |
| Т3-4 | С_06 полотенцесушитель | ½" | 1150 | ст. Г: 941 от А | обратка |

## Условные обозначения

- вывод В1 (код — в ведомости привязок)
- вывод Т3 (код — в ведомости привязок)
- вывод К1 (код — в ведомости привязок)
- сантехприбор по расстановке (габарит модели)
- чистовая поверхность стены (от неё привязки)
- стояк «Ст К1-N / Ст В1-N» (ГОСТ 21.601), Ø мм
- линия обрыва (граница фрагмента)
- А — обозначение стены А–Г (как на развёртках)

## Примечания


1. Привязки выводов даны от чистовых поверхностей стен (облицовка на сторону: санузел второго этажа — 24 мм (штукатурка 10 + клей 5 + плитка 9)); эти же грани — на развёртках и в раскладке плитки. Высоты — от чистого пола помещения.
2. До черновой разводки сверить по паспорту выбранного прибора (смеситель, инсталляция, сифон).
3. Горячая вода (Т3) — слева от холодной (В1), если смотреть на прибор. Допуск установки выводов: ±5 мм в группе, ±20 мм у отдельно стоящих.
4. Расчёт систем водоснабжения и канализации и подбор оборудования выполняет проектная организация; лист задаёт места и высоты выводов.
5. Стояки в коробах/шахтах не замоноличивать; стояк К1 в коробе — звукоизоляция стояка в коробе без жёсткого контакта с трубой; к арматуре и ревизиям — люк не меньше 300×400.

| | | | | | |
|---|---|---|---|---|---|
| | | | | | Проект: Дом 120 м² |
| | Лист | № док. | Подпись | Дата | План выводов сантехники · 2-й этаж |
| Дизайнер | Кырлан А.С. | | | 19.10.26 | |


| Стадия | Лист | Листов |
|---|---|---|
| П | 22 | 104 |

выпуск 19.10.2026 № 46d0102a0d · стр. 22 из 104


## План квартиры (М 1:200)

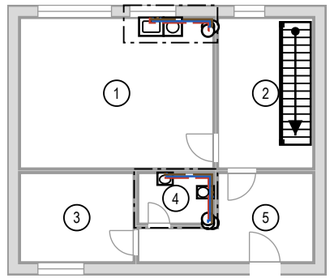


## Фр. 1. Санузел гостевой (М 1:25)

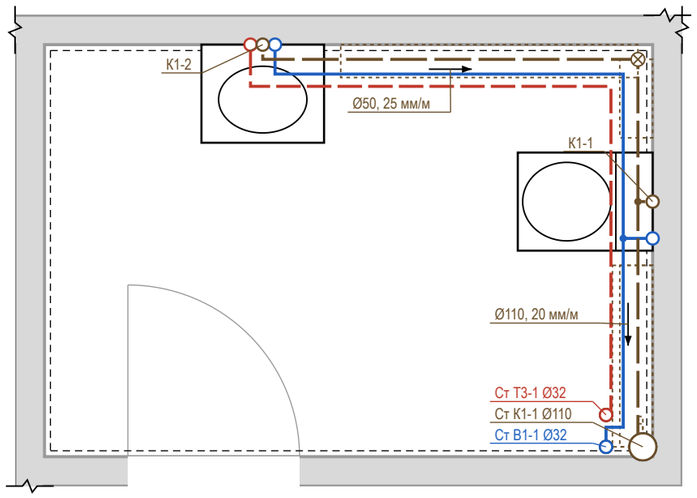


## Фр. 2. Гостиная-кухня (М 1:25)

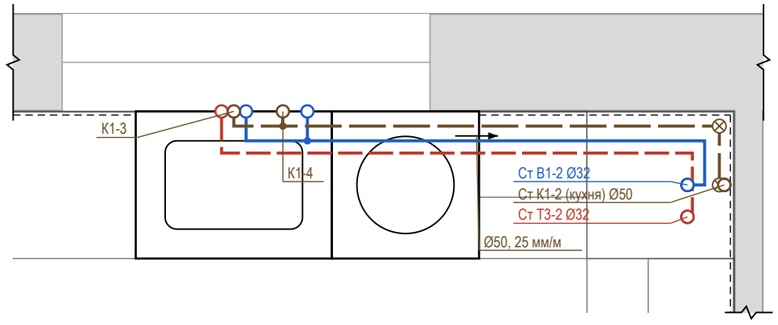


## Условные обозначения


- В1 — водопровод хозяйственно-питьевой (ХВС), PP-R Ø20
- Т3 — горячее водоснабжение, подача (ГВС), PP-R Ø20
- К1 — канализация бытовая
- направление уклона К1 / пола: Ø, мм на 1 м
- ревизия (прочистка) К1 — доступ сохранить
- тройник (ответвление к прибору)
- короб К1 над чистым полом (ГКЛВ под плитку)
- вывод В1 (код — в ведомости привязок)
- вывод Т3 (код — в ведомости привязок)
- вывод К1 (код — в ведомости привязок)
- сантехприбор по расстановке (габарит модели)
- стояк «Ст К1-N / Ст В1-N» (ГОСТ 21.601), Ø мм
- линия обрыва (граница фрагмента)
- граница фрагмента на плане (Фр. N)

## Профиль выпусков К1 (до врезки в стояк)

| Выпуск | Прибор | Ø | L, м | i, мм/м | Δh, мм | Прокладка, мм |
|---|---|---|---|---|---|---|
| К1-1 | С_01 унитаз подвесной | Ø110 | 1,08 | 20 | 22 | короб 170×140 |
| К1-2 | С_02 умывальник | Ø50 | 3,19 | 25 | 80 | короб 160×110 |
| К1-3 | П3 мойка кухонная | Ø50 | 2,30 | 25 | 58 | над полом за приборами |
| К1-4 | П4 посудомоечная машина | Ø40 | 2,10 | 30 | 63 | над полом за приборами |

Короб h×b: h — от чистого пола, b — от чистовой стены. Стяжка 35 мм — лист полов.

## Узел ввода В1, Т3 (схема, без масштаба)

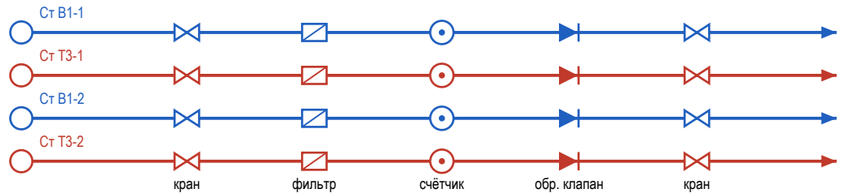


⊗ Ст К1-1, Ст К1-2 (кухня): ревизия на стояке — люк в коробе


## Примечания

1. Трассы принципиальные, построены от стояков вдоль стен помещений; фактическое положение фиксируется исполнительной схемой с привязками (фото с рулеткой) до закрытия.
2. Уклон К1 не менее 1/d и не более 150 мм/м (СП 30.13330.2020, п. 19.1), приняты практические уклоны; поворот — двумя отводами 45°, ревизия после поворота, доступ сохранить. Стояк К1 в коробе — звукоизоляция стояка в коробе, без жёсткого контакта короба с трубой.
3. Решение по К1: стяжка 35 мм не укрывает трубы (нужно Ø + Δh + 45 мм) — выпуски идут над чистым полом вдоль стен: К1-3, К1-4 — за приборами и в раме инсталляции; К1-1, К1-2 — в коробе ГКЛВ под плитку (размеры в профиле). Короба — на развёртках; отметку низа врезки в стояк замерить до черновых работ.
4. На каждом вводе В1 и Т3 — кран шаровой, фильтр, счётчик, обратный клапан; доступ через люк не меньше 300×400. Водопровод — в штробе стен или в коробах; трубы испытать давлением до закрытия (акт скрытых работ).
5. Расчёт систем, диаметры магистралей и подбор оборудования выполняет проектная организация; врезка и перенос стояков — по согласованию с управляющей организацией. Арматуру и привязки сверить по паспортам приборов.


| | | | | | |
|---|---|---|---|---|---|
| | | | | | Проект: Дом 120 м² |
| | Лист | № док. | Подпись | Дата | Схема разводки водопровода и канализации · 1-й этаж |
| Дизайнер | Кырлан А.С. | | | 19.10.26 | |

| Стадия | Лист | Листов |
|---|---|---|
| П | 23 | 104 |

## План квартиры (М 1:200)

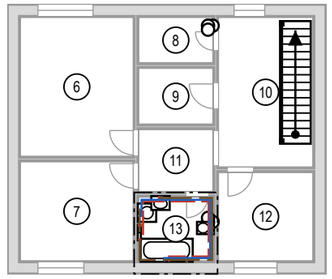


## Фр. 1. Санузел второго этажа (М 1:20)

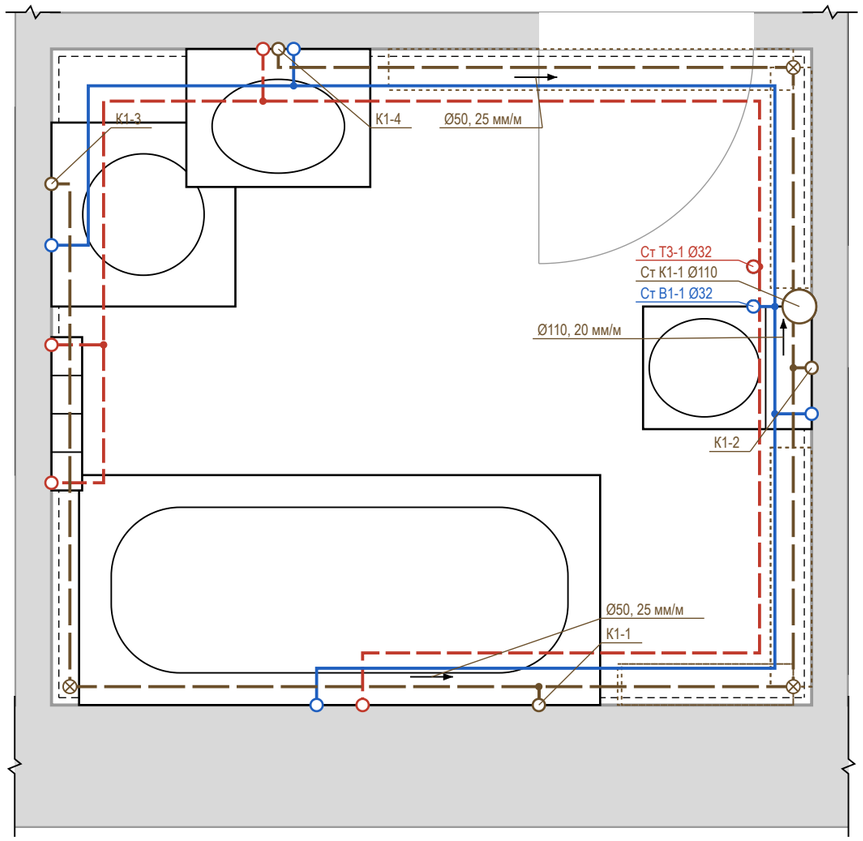


## Условные обозначения

- В1 — водопровод хозяйственно-питьевой (ХВС), PP-R Ø20
- Т3 — горячее водоснабжение, подача (ГВС), PP-R Ø20
- К1 — канализация бытовая
- направление уклона К1 / пола: Ø, мм на 1 м
- ревизия (прочистка) К1 — доступ сохранить
- тройник (ответвление к прибору)
- короб К1 над чистым полом (ГКЛВ под плитку)
- вывод В1 (код — в ведомости привязок)
- вывод Т3 (код — в ведомости привязок)
- вывод К1 (код — в ведомости привязок)
- сантехприбор по расстановке (габарит модели)
- стояк «Ст К1-N / Ст В1-N» (ГОСТ 21.601), Ø мм
- линия обрыва (граница фрагмента)
- граница фрагмента на плане (Фр. N)

## Профиль выпусков К1 (до врезки в стояк)

| Выпуск | Прибор | Ø | L, м | i, мм/м | Δh, мм | Прокладка, мм |
|---|---|---|---|---|---|---|
| К1-2 | С_04 унитаз подвесной | Ø110 | 0,28 | 20 | 6 | над полом за приборами |
| К1-3 | ОБ_02 стиральная машина | Ø50 | 5,32 | 25 | 133 | короб 220×110 |
| К1-4 | С_05 умывальник | Ø50 | 2,54 | 25 | 64 | под дверью — перенести выпуск |
| К1-1 | С_03 ванна | Ø50 | 2,15 | 25 | 54 | короб 140×110 |

Короб h×b: h — от чистого пола, b — от чистовой стены. Стяжка 35 мм — лист полов.

## Узел ввода В1, Т3 (схема, без масштаба)




⊗ Ст К1-1, Ст К1-2 (кухня): ревизия на стояке — люк в коробе

## Примечания

1. Трассы принципиальные, построены от стояков вдоль стен помещений; фактическое положение фиксируется исполнительной схемой с привязками (фото с рулеткой) до закрытия.
2. Уклон К1 не менее 1/d и не более 150 мм/м (СП 30.13330.2020, п. 19.1), приняты практические уклоны; поворот — двумя отводами 45°, ревизия после поворота, доступ сохранить. Стояк К1 в коробе — звукоизоляция стояка в коробе, без жёсткого контакта короба с трубой.
3. Решение по К1: стяжка 35 мм не укрывает трубы (нужно Ø + Δh + 45 мм) — выпуски идут над чистым полом вдоль стен: К1-2 — за приборами и в раме инсталляции; К1-3, К1-4, К1-1 — в коробе ГКЛВ под плитку (размеры в профиле). Короба — на развёртках; отметку низа врезки в стояк замерить до черновых работ.
4. Трасса К1 от К1-4 проходит под дверным проёмом — короб там невозможен: выпуск перенести или вести в полу с подъёмом пола помещения.
5. На каждом вводе В1 и Т3 — кран шаровой, фильтр, счётчик, обратный клапан; доступ через люк не меньше 300×400. Водопровод — в штробе стен или в коробах; трубы испытать давлением до закрытия (акт скрытых работ).
6. Расчёт систем, диаметры магистралей и подбор оборудования выполняет проектная организация; врезка и перенос стояков — по согласованию с управляющей организацией. Арматуру и привязки сверить по паспортам приборов.

| | | | | | |
|---|---|---|---|---|---|
| | | | | | Проект: Дом 120 м² |
| | Лист | № док. | Подпись | Дата | Схема разводки водопровода и канализации · 2-й этаж |
| Дизайнер | Кырлан А.С. | | | 19.10.26 | |

| Стадия | Лист | Листов |
|---|---|---|
| П | 24 | 104 |

выпуск 19.10.2026 № 46d0102a0d · стр. 24 из 104


| Поз. | Наименование и техническая характеристика | Тип, марка, обозначение документа | Код продукции | Поставщик | Ед. изм. | Кол. | Масса 1 ед., кг | Примечание |
|---|---|---|---|---|---|---|---|---|
| | Санитарные приборы | | | | | | | |
| 1 | Ванна акриловая 1700×750 мм, с каркасом, экраном и отверстием слив-перелив | аналог | | выбор заказчика | шт | 1 | | С_03 |
| 2 | Унитаз подвесной безободковый, с сиденьем микролифт, крепёж и звукоизолирующая прокладка | Jacob Delafon Struktura EDF102-00 | | выбор заказчика | шт | 2 | | С_01, С_04 |
| 3 | Инсталляция для подвесного унитаза: рама высотой 1120 мм, бачок, клавиша смыва (ось клавиши 1050 мм от чистого пола) | аналог | | выбор заказчика | шт | 2 | | С_01, С_04; короб ГКЛВ |
| 4 | Умывальник подвесной 500×400 мм, с отверстием под смеситель и переливом | аналог | | выбор заказчика | шт | 1 | | С_02 |
| 5 | Умывальник подвесной 600×450 мм, с отверстием под смеситель и переливом | аналог | | выбор заказчика | шт | 1 | | С_05 |
| 6 | Мойка кухонная 800×600 мм, с переливом | аналог | | с кухонной мебелью | шт | 1 | | П8 |
| 7 | Полотенцесушитель водяной (ГВС), с байпасом и кранами | аналог | | выбор заказчика | шт | 1 | | С_06 |
| | Смесители, сифоны и арматура приборов | | | | | | | |
| 8 | Смеситель для ванны настенный однорычажный, межосевое 150 мм, с душевым набором (лейка, шланг, держатель) | аналог | | выбор заказчика | шт | 1 | | С_03 |
| 9 | Смеситель для умывальника однорычажный, с донным клапаном | аналог | | выбор заказчика | шт | 2 | | С_02, С_05 |
| 10 | Смеситель кухонный однорычажный, высокий излив | аналог | | выбор заказчика | шт | 1 | | П8 |
| 11 | Обвязка ванны слив-перелив Ø40/50 с сифоном | аналог | | выбор заказчика | шт | 1 | | С_03 |
| 12 | Сифон для умывальника бутылочный Ø32/40–50, с гофрой к выпуску | аналог | | выбор заказчика | шт | 2 | | С_02, С_05 |
| 13 | Сифон для мойки с отводом для ПММ Ø40/50 | аналог | | выбор заказчика | шт | 1 | | П8 |
| 14 | Сифон для стиральной машины встраиваемый в стену Ø50, с обратным клапаном | аналог | | выбор заказчика | шт | 1 | | ОБ_02 |
| 15 | Кран угловой ½"×½" с гибкой подводкой 40 см (умывальники, мойка) | аналог | | выбор заказчика | шт | 6 | | по 2 на прибор |
| 16 | Кран шаровой угловой ½"×¾" для подключения стиральной и посудомоечной машины | аналог | | выбор заказчика | шт | 2 | | ОБ_02, П9 |
| 17 | Узел подключения полотенцесушителя: байпас Ду20, краны шаровые ½" ×2 | аналог | | выбор заказчика | шт | 1 | | |
| | Трубопроводы | | | | | | | |
| 18 | Труба полипропиленовая PP-R PN20 Ø20×3,4 (В1) | ГОСТ 32415-2013 | | выбор заказчика | м | 18,5 | 0,17 | 12,3 + 4,3 + 10 % |
| 19 | Труба PP-R, армированная стекловолокном, PN20 Ø20×2,8 (Т3) | ГОСТ 32415-2013 | | выбор заказчика | м | 19 | 0,15 | 12,0 + 4,9 + 10 % |
| 20 | Труба канализационная ПП Ø40 (К1) | ГОСТ 32414-2013 | | выбор заказчика | м | 1 | | 0,1 + 0,6 + 10 % |
| 21 | Труба канализационная ПП Ø50 (К1) | ГОСТ 32414-2013 | | выбор заказчика | м | 12,5 | | 9,3 + 2,0 + 10 % |
| 22 | Труба канализационная ПП Ø110 (К1) | ГОСТ 32414-2013 | | выбор заказчика | м | 2 | | 1,3 + 0,4 + 10 % |
| | Фасонные части и выводы | | | | | | | |
| 23 | Отвод канализационный ПП 45° Ø50 | ГОСТ 32414-2013 | | выбор заказчика | шт | 18 | | 2 шт. на поворот |
| 24 | Отвод канализационный ПП 45° Ø110 | ГОСТ 32414-2013 | | выбор заказчика | шт | 6 | | 2 шт. на поворот |
| 25 | Тройник канализационный ПП 45° (врезки ветвей) | ГОСТ 32414-2013 | | выбор заказчика | шт | 7 | | |
| 26 | Ревизия канализационная ПП (после поворота трассы) | ГОСТ 32414-2013 | | выбор заказчика | шт | 6 | | доступ сохранить |
| 27 | Фитинги PP-R Ø20: тройники, угольники 90° (ветви и повороты В1, Т3) | ГОСТ 32415-2013 | | выбор заказчика | шт | 36 | | |
| 28 | Водорозетка PP-R Ø20×½" настенная, с креплением | ГОСТ 32415-2013 | | выбор заказчика | шт | 14 | | коды — лист выводов |
| | Узлы ввода, люки, короба | | | | | | | |
| 29 | Кран шаровой латунный Ду15 PN16 (отключение ввода) | аналог | | выбор заказчика | шт | 4 | | Ст В1-1, Ст Т3-1, Ст В1-2, Ст Т3-2 |
| 30 | Фильтр сетчатый косой Ду15 | аналог | | выбор заказчика | шт | 4 | | |
| 31 | Счётчик воды крыльчатый Ду15 (ХВ, ГВ), с поверкой | аналог | | выбор заказчика | шт | 4 | | пломба УК |
| 32 | Клапан обратный Ду15 | аналог | | выбор заказчика | шт | 4 | | |
| 33 | Люк ревизионный нажимной под плитку 300×400 мм | аналог | | выбор заказчика | шт | 2 | | к стоякам и арматуре |
| 34 | Звукоизоляция стояка К1 в коробе: рулонный звукоизоляционный материал ≥ 10 мм, обмотка стояка на высоту этажа | аналог | | выбор заказчика | м | 5,8 | | Ст К1-1, Ст К1-2 (кухня) |
| 35 | Короб К1 над полом: профиль ПН/ПС, ГКЛВ 12,5 мм под плитку | аналог | | выбор заказчика | м | 9,9 | | сечение — лист разводки |

## Примечания

1. Форма 1 ГОСТ 21.110-2013, ширины граф изменены по п. 4.1. «Аналог» — аналог по характеристикам: модели внести до черновых работ, привязки выводов сверить по паспортам.
2. Бытовая техника не входит (показана арматура подключения), мойка — в комплекте кухни. Длины труб — трасса листа разводки + подъёмы + 10 %.
3. Стояк К1 в коробе — звукоизоляция стояка в коробе без жёсткого контакта короба с трубой.
4. Расчёт систем водоснабжения и канализации, диаметры магистралей и подбор оборудования выполняет проектная организация.

| | | | | | Проект: Дом 120 м² | | | |
|---|---|---|---|---|---|---|---|---|
| | Лист | № док. | Подпись | Дата | Спецификация сантехнического оборудования | Стадия | Лист | Листов |
| Дизайнер | Кырлан А.С. | | | 19.10.26 | | П | 25 | 104 |

выпуск 19.10.2026 № 46d0102a0d · стр. 25 из 104

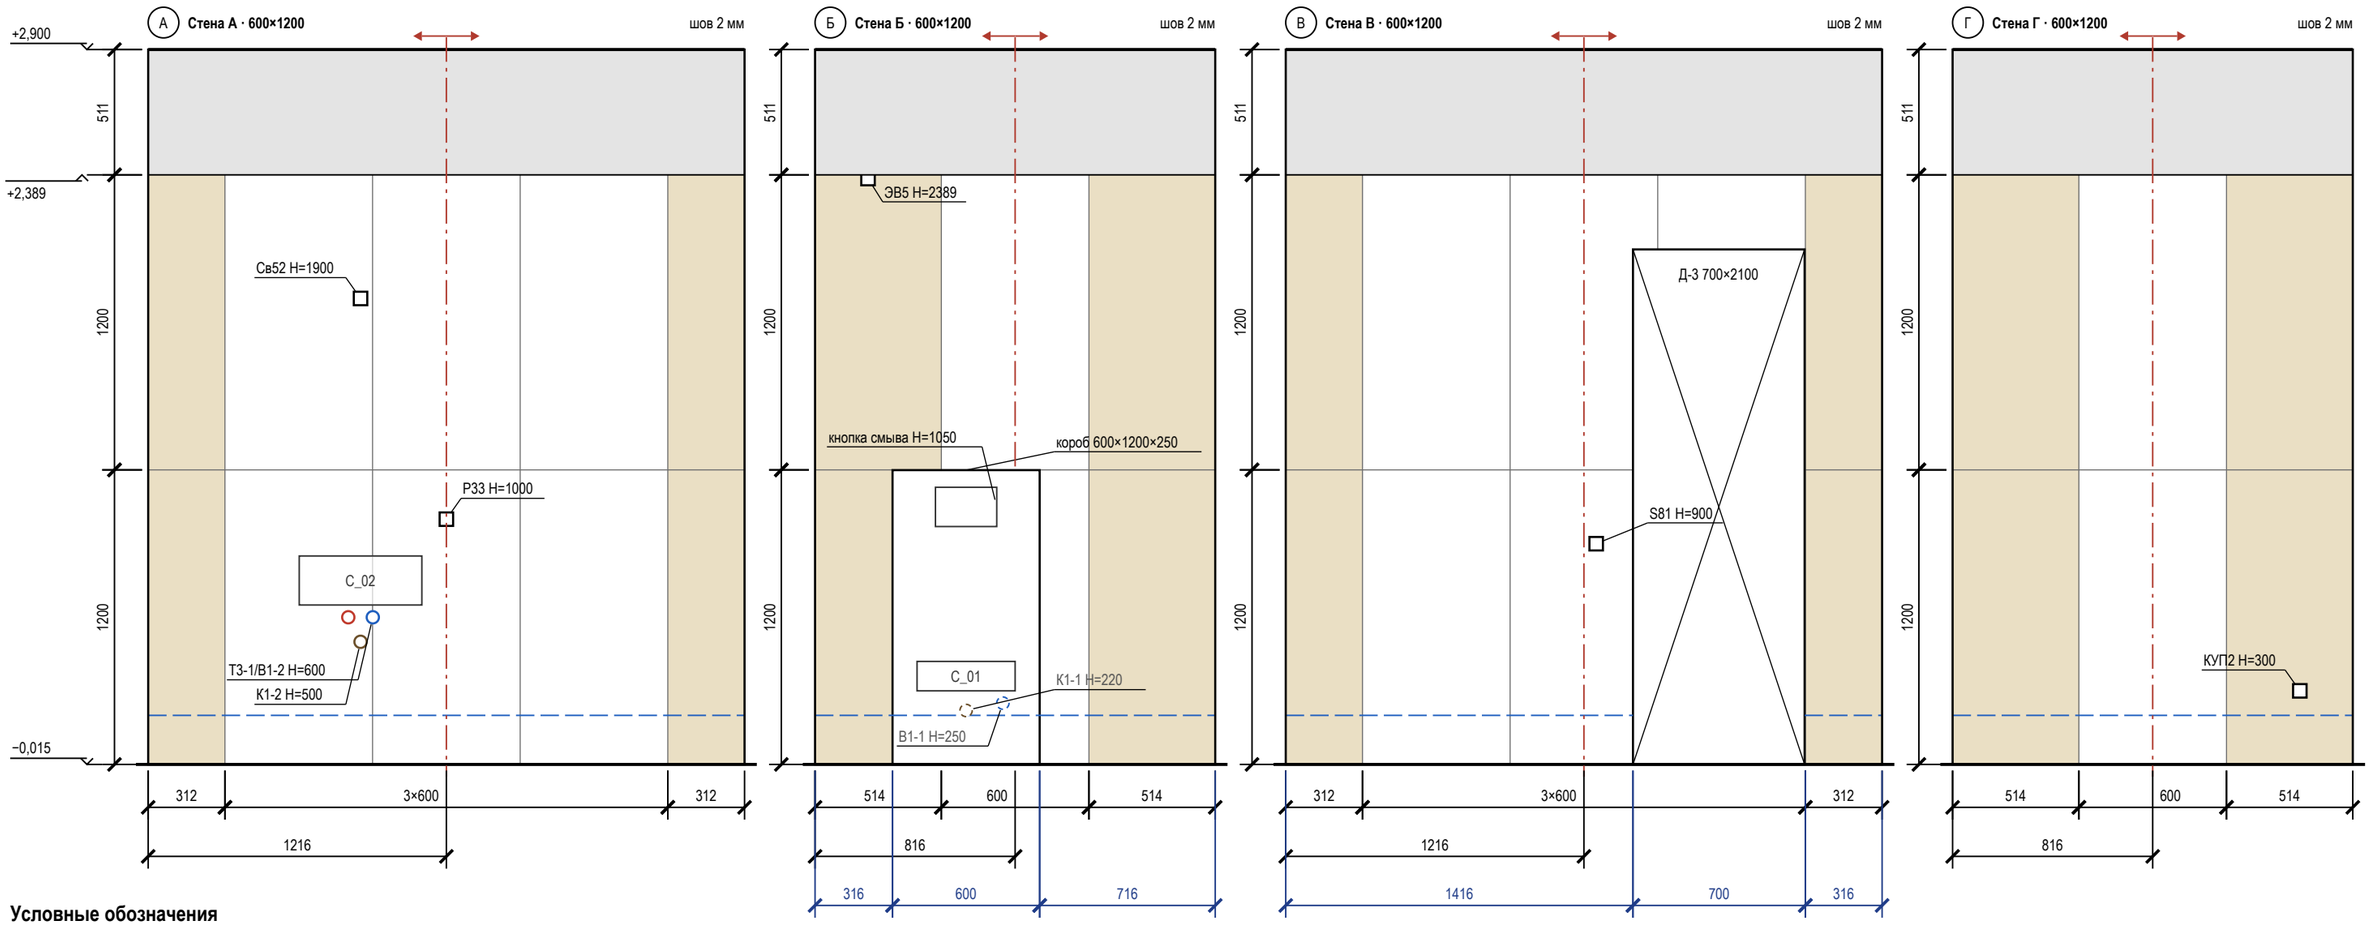


## Условные обозначения

- плитка целая; тонкая линия — шов
- плитка с подрезкой (размер — на цепочке)
- ось старта; стрелки — направление укладки
- верх гидроизоляции: 200 от ЧП, в мокрой зоне — «до …»
- проём — не облицовывается
- сантехприбор: габарит, высота по практике
- короб инсталляции, в нём кнопка смыва 250×160
- вывод В1 (код — в ведомости привязок)
- вывод Т3 (код — в ведомости привязок)
- вывод К1 (код — в ведомости привязок)
- вывод за прибором / в коробе (не на сетке)
- электроточка: марка и H — по листам ЭОМ
- отметка уровня, м: ±0,000 — чистый пол жилых помещений
- низ потолка; серая полоса — стена без плитки
- (А) обозначение стены А–Г (как на развёртках)

## Подсчёт плитки по стенам и коробу

| Поверхность | L × H, мм | S, м² | Целых | Подр. | С запасом | Подрезки: край / верх, мм |
|---|---|---|---|---|---|---|
| стена А | 2432 × 2404 | 5,96 | 6 | 4 | 11 | 312 / 312; целый ряд |
| стена Б | 1632 × 2404 | 3,32 | 1 | 5 | 7 | 514 / 514; целый ряд |
| короб (ст. Б) | 600×1200×250 | 1,47 | 1 | 3 | 5 | лицо 600; бок. 250 |
| стена В | 2432 × 2404 | 4,49 | 2 | 8 | 11 | 312 / 312; целый ряд |
| стена Г | 1632 × 2404 | 2,90 | 2 | 4 | 7 | 514 / 514; целый ряд |
| **Итого** | | **18,15** | **12** | **24** | **41** | |

## Сдвиг точек под раскладку

| Точка (ВК, ЭОМ) | Стена | Проект: от угла / H | Под раскладку: от угла / H | Сдвиг, мм |
|---|---|---|---|---|
| Т3-1/В1-2, К1-2, Св52 | А | 866 / 600, 500, 1900 | 915 / 600, 500, 1900 | +49 на шов |
| ЭВ5 | Б | 216 / 2389 | 216 / 2403 | H +14 |
| S81 | В | 1266 / 900 | 1216 / 900 | −50 в центр плитки |


## Примечания

1. Вид изнутри, стены по часовой стрелке А → Г. Высоты — от чистого пола (−0,015), отметки от ±0,000. Раскладка от чистовых размеров (штукатурка 10 + клей 5 + плитка 9 мм), подрезки чистые; старт — от оси стены, ряды от пола целыми.
2. Верх плитки +2,389, потолок +2,900, зазор 511 мм: потолок ГКЛ опустить до +2,392 (шов 3 мм, герметик) — согласовать с монтажником ГКЛ; иначе профиль-окантовка, полосу окрасить в цвет потолка. Подрезной ряд 506 мм не делать.
3. Точки из таблицы сдвигов переносятся до черновой разводки: смеситель — по оси пары В1 + Т3; вывод на оси прибора — вместе с прибором, иначе старт раскладки — на ось прибора.
4. За приборами и в коробе (В1-1, К1-1) — штриховым кольцом.
5. Гидроизоляция: 200 мм от ЧП по периметру; углы — лентой; акт скрытых работ, пролив.
6. Короб 600×1200×250: лицо 600 мм от оси кнопки смыва, боковины, полка; углы — запил 45° или профиль; за коробом плитку не кладут.

| | | | | | |
|---|---|---|---|---|---|
| | | | | | Проект: Дом 120 м² |
| | Лист | № док. | Подпись | Дата | Раскладка плитки. Санузел гостевой. Развёртки стен |
| Дизайнер | Кырлан А.С. | | | 19.10.26 | |

| Стадия | Лист | Листов |
|---|---|---|
| П | 26 | 104 |

выпуск 19.10.2026 № 46d0102a0d · стр. 26 из 104

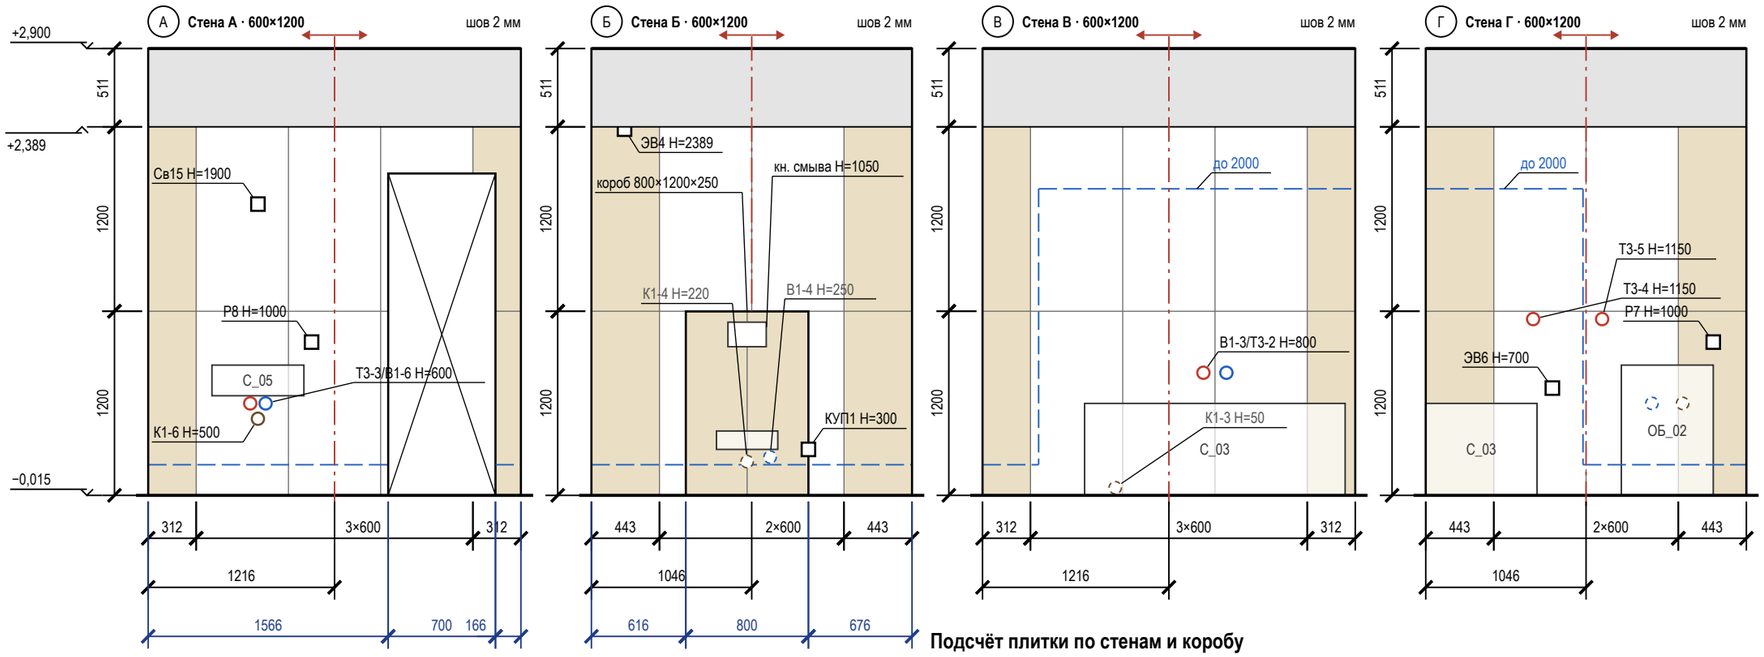


## Примечания

1. Вид изнутри, стены по часовой стрелке А → Г. Высоты — от чистого пола (−0,015), отметки — от ±0,000. Раскладка от чистовых размеров (штукатурка 10 + клей 5 + плитка 9 мм), подрезки чистые; старт — от оси стены, ряды от пола целыми.
2. Верх плитки +2,389, потолок +2,900, зазор 511 мм: потолок ГКЛ опустить до +2,392 (шов 3 мм, герметик) согласовать с монтажником ГКЛ; иначе профиль-окантовка, полосу окрасить в цвет потолка. Подрезной ряд 506 мм не делать.
3. Точки из таблицы сдвигов переносятся до черновой разводки: смеситель — по оси пары В1 + Т3; вывод на оси прибора — вместе с прибором, иначе старт раскладки — на ось прибора.
4. За приборами и в коробе (В1-4, К1-4, К1-3, В1-5, К1-5) — штриховым кольцом.
5. Гидроизоляция: 200 мм от ЧП по периметру; над ванной — до 2000 и 300 мм за борт (СП 29.13330.2011, п. 7.2 — на высоту замачивания); углы — лентой; акт скрытых работ, пролив.
6. Короб 800×1200×250: лицо 399 / 399 мм от оси кнопки смыва, боковины, полка; углы — запил 45° или профиль; за коробом плитку не кладут.
7. Линии узора (швы плитки, складки штор, рёбра радиаторов) прерываются у знаков и выносок — просвет между линиями не менее 0,7 мм.

## Подсчёт плитки по стенам и коробу

| Поверхность | L × H, мм | S, м² | Целых | Подр. | С запасом | Подрезки: край / верх, мм |
|---|---|---|---|---|---|---|
| стена А | 2432 × 2404 | 4,49 | 4 | 6 | 11 | 312 / 312; целый ряд |
| стена Б | 2092 × 2404 | 4,18 | 2 | 6 | 9 | 443 / 443; целый ряд |
| короб (ст. Б) | 800×1200×250 | 1,76 | 0 | 6 | 7 | лицо 399 / 399; бок. 250 |
| стена В | 2432 × 2404 | 5,96 | 6 | 4 | 11 | 312 / 312; целый ряд |
| стена Г | 2092 × 2404 | 3,46 | 4 | 4 | 9 | 443 / 443; целый ряд |
| **Итого** | | **19,86** | **16** | **26** | **47** | |

## Сдвиг точек под раскладку

| Точка (ВК, ЭОМ) | Стена | Проект: от угла / Н | Под раскладку: от угла / Н | Сдвиг, мм |
|---|---|---|---|---|
| Т3-3/В1-6, К1-6, Св15 | А | 716 / 600, 500, 1900 | 614 / 600, 500, 1900 | −102 в центр плитки |
| Р8 | А | 1066 / 1000 | 1216 / 1000 | +150 в центр плитки |
| ЭВ4 | Б | 216 / 2389 | 143 / 2403 | −73 в центр плитки; Н +14 |
| КУП1 | Б | 1416 / 300 | 1347 / 300 | −69 в центр плитки |
| Т3-4 | Г | 701 / 1150 | 745 / 1150 | +44 в центр плитки |
| Т3-5 | Г | 1151 / 1150 | 1046 / 1150 | −105 на шов |
| Р7 | Г | 1876 / 1000 | 1949 / 1000 | +73 в центр плитки |
| ЭВ6 | Г | 826 / 700 | 745 / 700 | −81 в центр плитки |


## Условные обозначения

- плитка целая; тонкая линия — шов
- плитка с подрезкой (размер — на цепочке)
- ось старта; стрелки — направление укладки
- верх гидроизоляции: 200 от ЧП, в мокрой зоне — «до …»
- проём — не облицовывается
- сантехприбор: габарит, высота по практике
- короб инсталляции, в нём кнопка смыва 250×160
- вывод В1 (код — в ведомости привязок)
- вывод Т3 (код — в ведомости привязок)
- вывод К1 (код — в ведомости привязок)
- вывод за прибором / в коробе (не на сетке)
- электроточка: марка и Н — по листам ЭОМ
- отметка уровня, м: ±0,000 — чистый пол жилых помещений
- низ потолка; серая полоса — стена без плитки
- А — обозначение стены А–Г (как на развёртках)

| | | | | | |
|---|---|---|---|---|---|
| | | | | | Проект: Дом 120 м² |
| | Лист | № док. | Подпись | Дата | Раскладка плитки. Санузел второго этажа. Развёртки стен |
| Дизайнер | Кырлан А.С. | | | 19.10.26 | |

| Стадия | Лист | Листов |
|---|---|---|
| П | 27 | 104 |

выпуск 19.10.2026 № 46d0102a0d · стр. 27 из 104

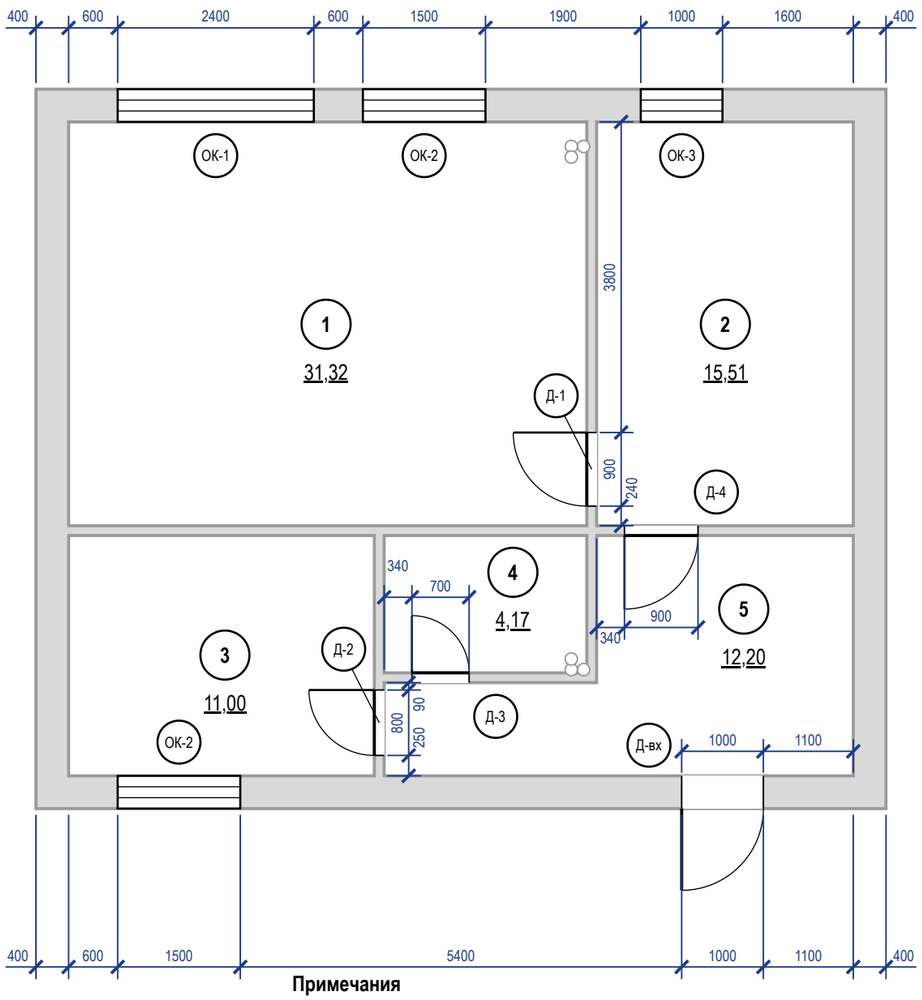


## Ведомость заполнения проёмов

| Марка | Наименование, обозначение | Проём ш×в, мм | Кол. | Откр. | Отделка полотна | Фурнитура | Прим. |
|---|---|---|---|---|---|---|---|
| Д-вх | Блок дверной входной, ГОСТ 31173-2016 | 1000×2100 | 1 | Л | в комплекте блока | в комплекте блока (замки, глазок) | наружу |
| Д-1 | Дверь скрытого монтажа, ТУ изготовителя | 900×2100 | 1 | Л | окраска G503 с двух сторон | скрытые петли 3D, магнитный замок | |
| Д-2 | Дверь скрытого монтажа, ТУ изготовителя | 800×2100 | 1 | Л | окраска G503 с двух сторон | скрытые петли 3D, магнитный замок | |
| Д-3 | Дверь скрытого монтажа, ТУ изготовителя | 700×2100 | 1 | П | в тон облицовки — пом. 4, G503 — пом. 5 | скрытые петли 3D, магнитный замок, фиксатор WC | порог 15 |
| Д-4 | Дверь скрытого монтажа, ТУ изготовителя | 900×2100 | 1 | Л | окраска G503 с двух сторон | скрытые петли 3D, магнитный замок | |
| ОК-1 | Блок оконный, ГОСТ 23166-2021; стекло — триплекс | 2400×1900 | 1 | | | | низ 500 |
| ОК-2 | Блок оконный, ГОСТ 23166-2021 | 1500×1500 | 2 | | | | низ 900 |
| ОК-3 | Блок оконный, ГОСТ 23166-2021 | 1000×1500 | 1 | | | | низ 900 |


## Примечания

1. Размеры проёмов и привязки — в миллиметрах от чистых граней стен до отделки; привязка — от угла того помещения, со стороны которого стоит размер. Размер в ведомости — ширина × высота проёма от чистого пола 0,000. Откос от угла помещения до проёма с коробкой — не менее 50 мм.
2. Марки в кружках — типы заполнения проёмов (ГОСТ 21.501-2018, п. 5.3.2); одна марка — один типоразмер; количество сверено с планом.
3. Открывание: Л — петли слева, П — справа, если смотреть со стороны, куда открывается полотно (на себя).
4. Остекление окон: ОК-1 (пом. 1) — триплекс. Тип стекла указать при заказе оконных блоков; замена на другое стекло — только по согласованию с автором проекта.
5. ОК-1: низ остекления 500 мм — ниже 900 мм от чистого пола, поэтому окно заказывать с безопасным стеклом (триплекс); ограждение проёма в проекте не задано (СП 54.13330.2022, п. 6.4.9; ГОСТ Р 56926).
6. Скрытые двери (Д-1…Д-4): проём замерить в чистоте; блок заказать до штукатурки (≈ 30 дн.), короб ставить до штукатурки; полотно навесить после чистовой отделки, красить в цвет стен. Порядок практика монтажа, изготовитель подтверждает.
7. Д-1…Д-4 — существующие проёмы, до техзаключения не расширять.

| | | | | | |
|---|---|---|---|---|---|
| | | | | | Проект: Дом 120 м² |
| | Лист | № док. | Подпись | Дата | План размещения дверей · 1-й этаж |
| Дизайнер | Кырлан А.С. | | | 19.10.26 | |

| Стадия | Лист | Листов |
|---|---|---|
| П | 28 | 104 |

выпуск 19.10.2026 № 46d0102a0d · стр. 28 из 104

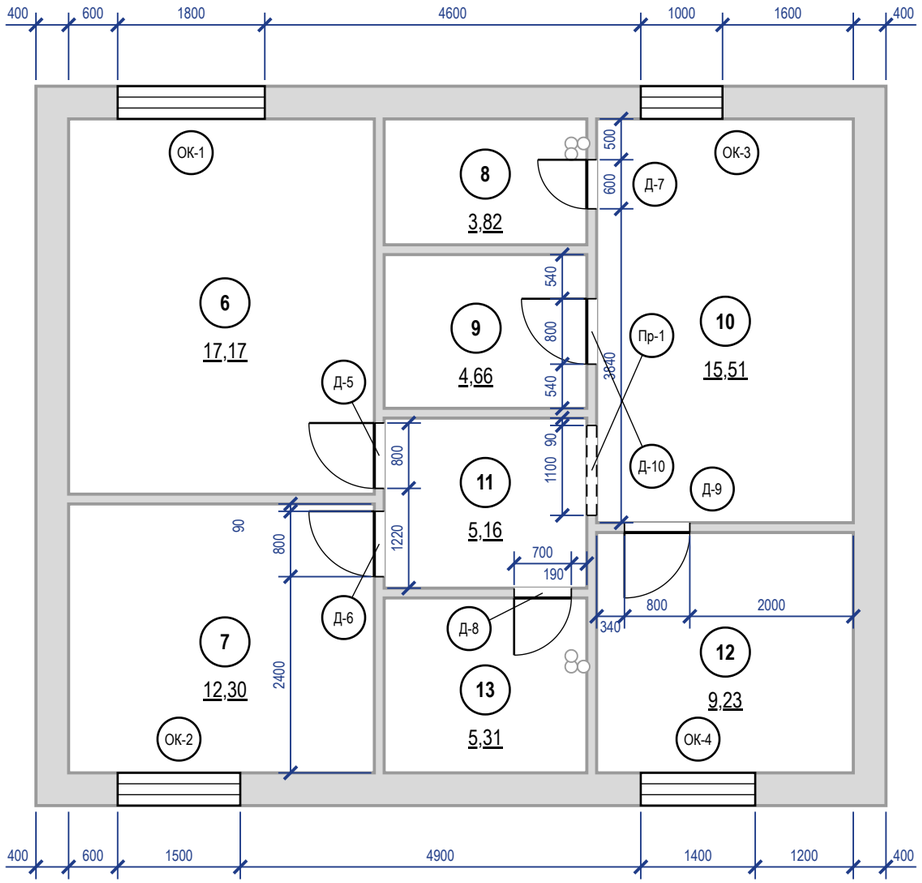


## Ведомость заполнения проёмов

| Марка | Наименование, обозначение | Проём ш×в, мм | Кол. | Откр. | Отделка полотна | Фурнитура | Прим. |
|---|---|---|---|---|---|---|---|
| Д-5 | Дверь скрытого монтажа, ТУ изготовителя | 800×2100 | 1 | Л | окраска G503 с двух сторон | скрытые петли 3D, магнитный замок | |
| Д-6 | Дверь скрытого монтажа, ТУ изготовителя | 800×2100 | 1 | Л | окраска G503 с двух сторон | скрытые петли 3D, магнитный замок | |
| Д-7 | Дверь скрытого монтажа, ТУ изготовителя | 600×2100 | 1 | Л | No. 222 — пом. 8, G503 — пом. 10 | скрытые петли 3D, магнитный замок | |
| Д-8 | Дверь скрытого монтажа, ТУ изготовителя | 700×2100 | 1 | Л | в тон облицовки — пом. 13, G503 — пом. 11 | скрытые петли 3D, магнитный замок, фиксатор WC | порог 15 |
| Д-9 | Дверь скрытого монтажа, ТУ изготовителя | 800×2100 | 1 | Л | окраска G503 с двух сторон | скрытые петли 3D, магнитный замок | |
| Д-10 | Дверь скрытого монтажа, ТУ изготовителя | 800×2100 | 1 | Л | S 0502-Y — пом. 9, G503 пом. 10 | скрытые петли 3D, магнитный замок | |
| Пр-1 | Портал без заполнения | 1100×2100 | 1 | | | | б/п |
| ОК-1 | Блок оконный, ГОСТ 23166-2021 | 1800×1500 | 1 | | | | низ 900 |
| ОК-2 | Блок оконный, ГОСТ 23166-2021 | 1500×1450 | 1 | | | | низ 900 |
| ОК-3 | Блок оконный, ГОСТ 23166-2021 | 1000×1500 | 1 | | | | низ 900 |
| ОК-4 | Блок оконный, ГОСТ 23166-2021 | 1400×1450 | 1 | | | | низ 900 |


## Примечания

1. Размеры проёмов и привязки — в миллиметрах от чистых граней стен до отделки; привязка — от угла того помещения, со стороны которого стоит размер. Размер в ведомости — ширина × высота проёма от чистого пола 0,000. Откос от угла помещения до проёма с коробкой — не менее 50 мм.
2. Марки в кружках — типы заполнения проёмов (ГОСТ 21.501-2018, п. 5.3.2); одна марка — один типоразмер; количество сверено с планом.
3. Открывание: Л — петли слева, П — справа, если смотреть со стороны, куда открывается полотно (на себя).
4. Скрытые двери (Д-5…Д-10): проём замерить в чистоте; блок заказать до штукатурки (≈ 30 дн.), короб ставить до штукатурки; полотно навесить после чистовой отделки, красить в цвет стен. Порядок практика монтажа, изготовитель подтверждает.
5. Д-5…Д-10 — существующие проёмы, до техзаключения не расширять.
6. Привязка проёма к углу помещения меньше 1 мм на листе, размер на плане не показан: Д-5 — 60 мм.


| | | | | | Проект: Дом 120 м² | | | |
|---|---|---|---|---|---|---|---|---|
| | Лист | № док. | Подпись | Дата | План размещения дверей · 2-й этаж | Стадия | Лист | Листов |
| Дизайнер | Кырлан А.С. | | | 19.10.26 | | П | 29 | 104 |

выпуск 19.10.2026 № 46d0102a0d · стр. 29 из 104

## План марша Л-1 (М 1:50) · 2. Холл с лестницей

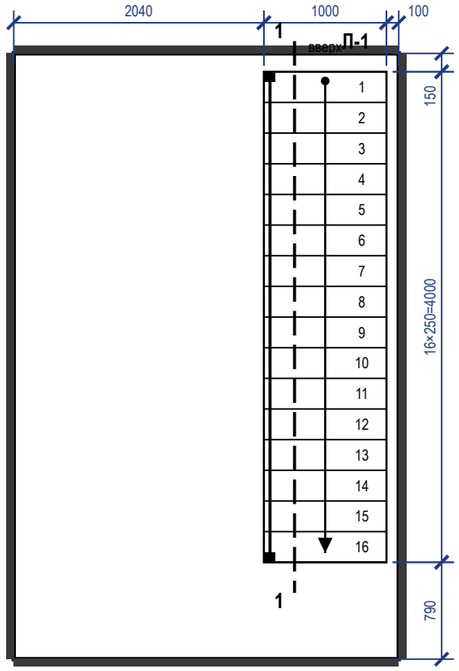



## Разрез 1-1 (М 1:50)

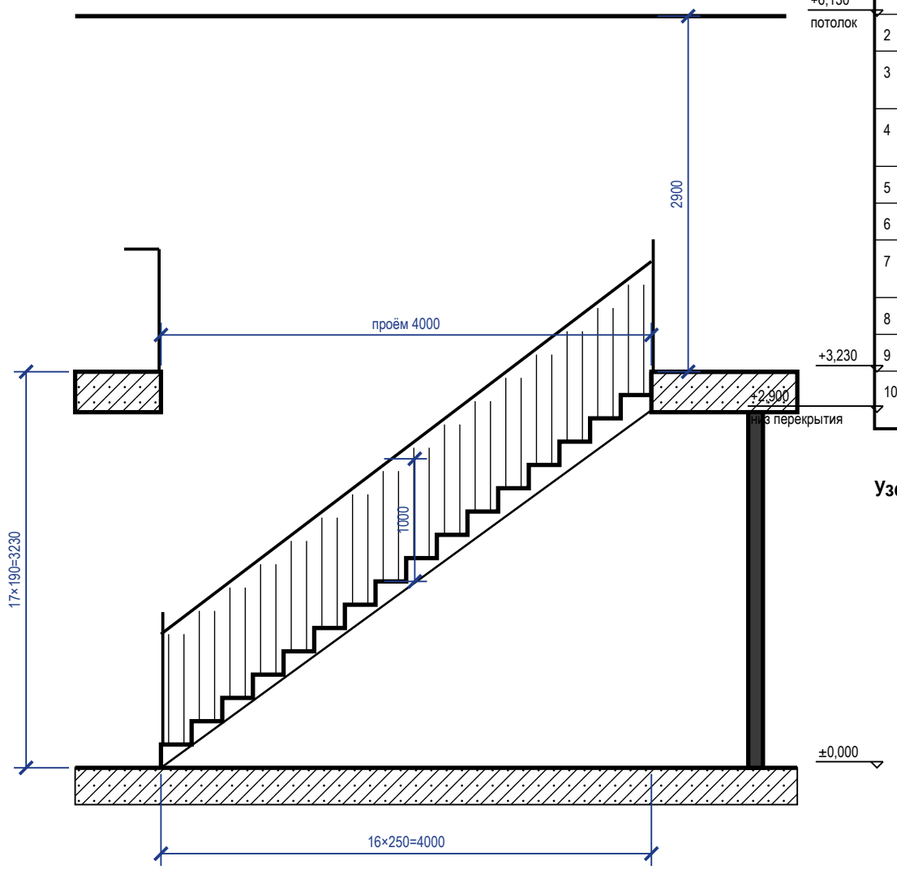


## Спецификация элементов лестницы Л-1

| Поз. | Наименование | Кол. | Материал, сечение | Примечание |
|---|---|---|---|---|
| 1 | Ступень (проступь) | 16 | дуб табак, 40 мм | 1000×250, толщина по изделию |
| 2 | Подступенок | 17 | дуб табак | высота 190 |
| 3 | Косоур | 2 | косоуры стальные, тёплый графит | несущие марша |
| 4 | Столб ограждения марша | 2 | дуб табак, стойки — графит | по концам марша, стороны Г |
| 5 | Балясина | 45 | дуб табак, стойки — графит | шаг 110, просвет 80 |
| 6 | Поручень марша | 1 | Ø40 | L ≈ 5,02 м, h 900 |
| 7 | Столб ограждения проёма | 2 | дуб табак, стойки — графит | углы проёма, стороны Г |
| 8 | Балясина ограждения проёма | 36 | дуб табак, стойки — графит | шаг 110 |
| 9 | Поручень ограждения проёма | 1 | Ø40 | L ≈ 4,00 м, h 1000 |
| 10 | Крепёж ограждения | 1 | комплект по изделию | нагрузка на поручень 0,5 кН/м |

## Узел 1. Крепление стойки ограждения (М 1:5)

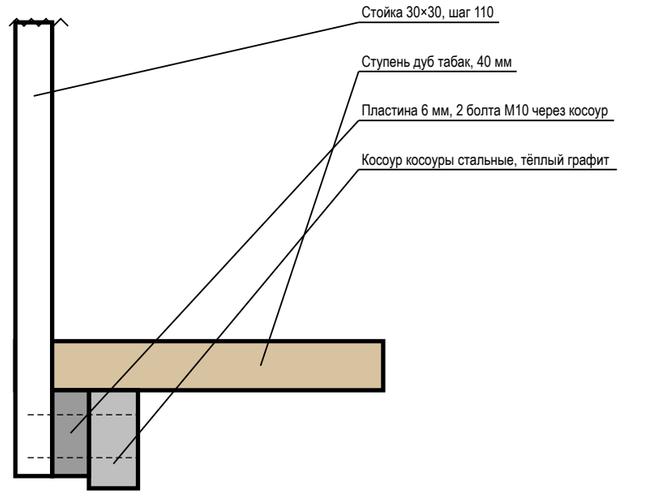


Зазор заполнения до ступени 100 (ГОСТ 25772, прил. А); узел типовой, уточнить по изделию

## Примечания

1. Лестница Л-1: 17 подъёмов × 190 мм = 3230 мм (отм. ±0,000 … +3,230), проступь 250 мм, ширина марша 1000 мм; уклон 37,2°, шаг 2h + b = 630 мм (удобно 600–640 — практика).
2. Ограждение марша со стороны Г: балясины, просвет между элементами 80 мм (не больше 150 — ГОСТ 25772-2025, табл. 3, тип МВ); высота 1000 мм, поручень с одной стороны на 900 мм по линии носков (не менее 900 — СП 55.13330.2016, п. 8.3; СП 59.13330.2020, п. 6.2.11).
3. Проём в перекрытии 1000×4000 мм на этаже 2 ограждён со сторон Г высотой 1000 мм, непрерывно, с поручнем (СП 55.13330.2016, п. 8.3); нагрузка на поручень 0,5 кН/м (СП 20.13330.2016, п. 8.2.6).
4. Просвет над линией носков — не менее 2900 мм (ступень 17, под потолком мансарды); рекомендуется не менее 2000, путь эвакуации — 2200 (СП 55.13330.2016, п. 7.4).
5. Все подступенки одной высоты (СП 55.13330.2016, п. 8.2). Размеры по месту уточнить после обмера: разность отметок чистых полов замерить до заказа изделия.
6. Узел 1 — типовое решение крепления стойки к косоуру; крепёж, сечения и материал — по проекту изделия изготовителя лестницы.


| | | | | |
|---|---|---|---|---|
| | Лист | № док. | Подпись | Дата |
| Дизайнер | Кырлан А.С. | | | 19.10.26 |

Проект: Дом 120 м²

Лестница Л-1

| Стадия | Лист | Листов |
|---|---|---|
| П | 30 | 104 |

выпуск 19.10.2026 № 46d0102a0d · стр. 30 из 104

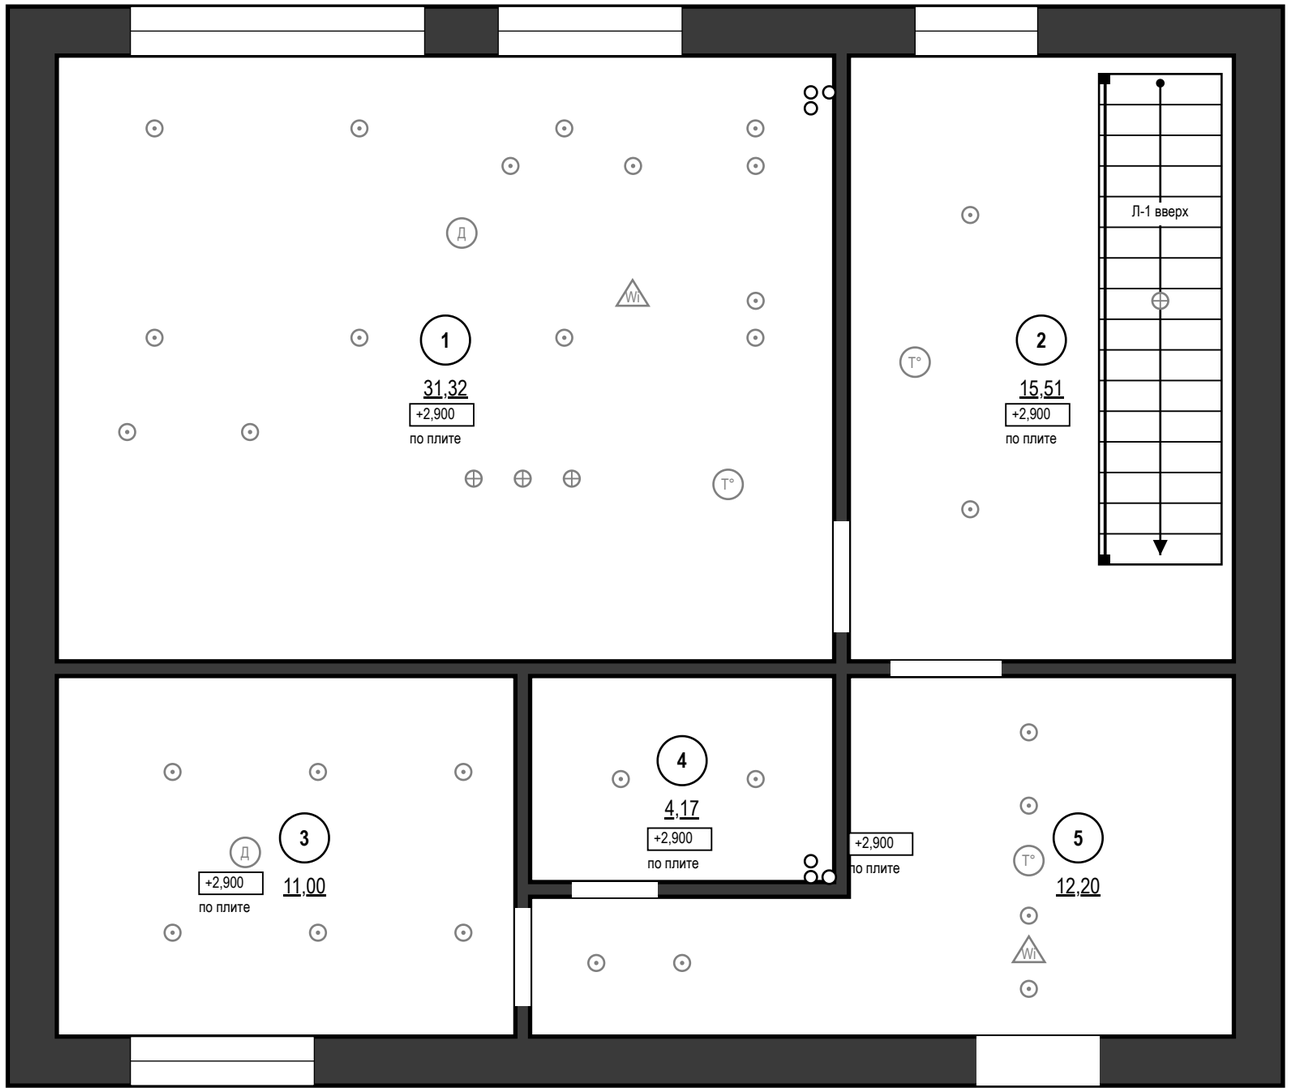


## Ведомость потолков

| Пом. | Марка | Конструкция | Низ | S, м² | Q |
|---|---|---|---|---|---|
| 1 | | по плите, окраска | +2,900 | 31,32 | |
| 2 | | по плите, окраска | +2,900 | 15,51 | |
| 3 | | по плите, окраска | +2,900 | 11,00 | |
| 4 | | по плите, окраска | +2,900 | 4,17 | |
| 5 | | по плите, окраска | +2,900 | 12,20 | |
| | | **Итого** | | **74,20** | |

## Ведомость вырезов и закладных в потолке

| Марка | Устройство | Кол. | Пом. |
|---|---|---|---|
| | Светильник встраиваемый (марки — план освещения) | 30 | 1, 2, 3, 4, 5 |
| | Светильник подвесной (марки — план освещения) | 4 | 1, 2 |
| ИП4, ИП2 | Извещатель дымовой | 2 | 1, 3 |
| ИП5, ИП6, ИП3 | Извещатель тепловой | 3 | 1, 2, 5 |
| АР2, АР1 | Точка доступа Wi-Fi, PoE | 2 | 1, 5 |


## Примечания

1. За отметку ±0,000 принят уровень чистого пола сухих помещений (готовое покрытие), а не существующего пола; пол пом. 4 — −0,015; верх плиты перекрытия −0,064 — расчётный по пирогу пола, не замерен; существующий пол снимается до плиты, его отметка не замерена. Отметки в прямоугольниках — низ потолка; низ плиты перекрытия +2,900. Марка потолка — одна конструкция и отметка на весь альбом.
2. Светильники и потолочные устройства — подложка с планов освещения, слаботочных систем и вентиляции (положение — по ним); вырезы и закладные — по ведомости на листе, до обшивки; отверстия не совмещать с профилями.
3. Пом. 1, 2, 3, 4, 5 — потолок по плите без подвесной системы; отделка — по ведомости отделки.

| | | | | | |
|---|---|---|---|---|---|
| | | | | | Проект: Дом 120 м² |
| | Лист | № док. | Подпись | Дата | План потолков · 1-й этаж |
| Дизайнер | Кырлан А.С. | | | 19.10.26 | |

| Стадия | Лист | Листов |
|---|---|---|
| П | 31 | 104 |

выпуск 19.10.2026 № 46d0102a0d · стр. 31 из 104

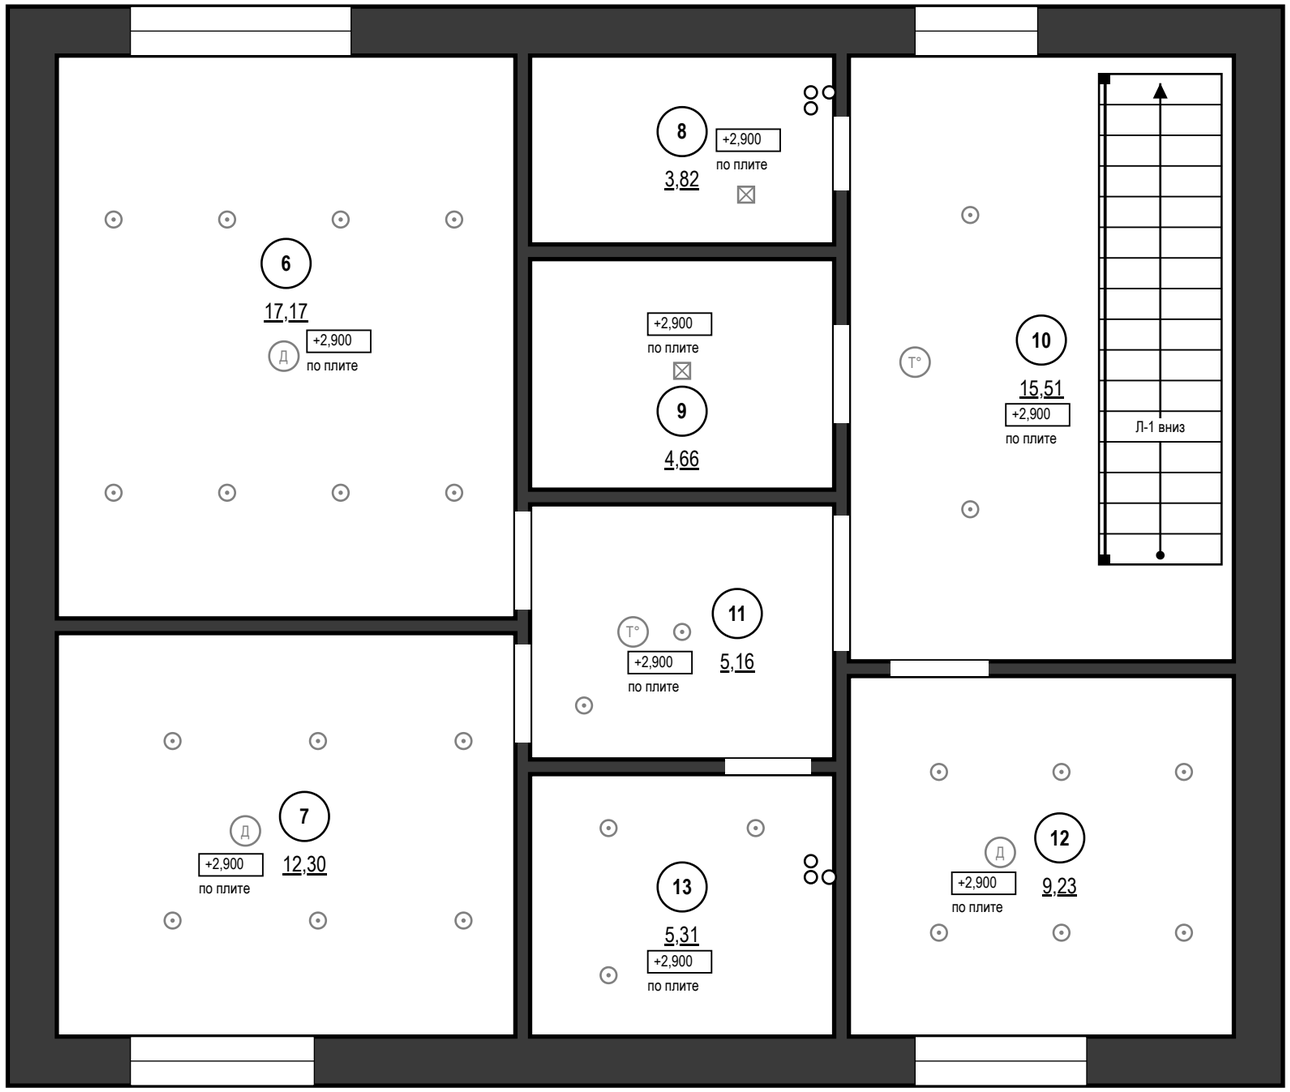


## Ведомость потолков

| Пом. | Марка | Конструкция | Низ | S, м² | Q |
|---|---|---|---|---|---|
| 6 | | по плите, окраска | +2,900 | 17,17 | |
| 7 | | по плите, окраска | +2,900 | 12,30 | |
| 8 | | по плите, окраска | +2,900 | 3,82 | |
| 9 | | по плите, окраска | +2,900 | 4,66 | |
| 10 | | по плите, окраска | +2,900 | 15,51 | |
| 11 | | по плите, окраска | +2,900 | 5,16 | |
| 12 | | по плите, окраска | +2,900 | 9,23 | |
| 13 | | по плите, окраска | +2,900 | 5,31 | |
| | | **Итого** | | **73,16** | |

## Ведомость вырезов и закладных в потолке

| Марка | Устройство | Кол. | Пом. |
|---|---|---|---|
| | Светильник встраиваемый (марки — план освещения) | 27 | 6, 7, 10, 11, 12, 13 |
| | Светильник накладной (марки — план освещения) | 2 | 8, 9 |
| ИП1, ИП2, ИП2 | Извещатель дымовой | 3 | 6, 7, 12 |
| ИП6, ИП7 | Извещатель тепловой | 2 | 10, 11 |


## Примечания

1. За отметку ±0,000 принят уровень чистого пола сухих помещений (готовое покрытие), а не существующего пола; пол пом. 13 — −0,015; верх плиты перекрытия −0,064 — расчётный по пирогу пола, не замерен; существующий пол снимается до плиты, его отметка не замерена. Отметки в прямоугольниках — низ потолка; низ плиты перекрытия +2,900. Марка потолка — одна конструкция и отметка на весь альбом.
2. Светильники и потолочные устройства — подложка с планов освещения, слаботочных систем и вентиляции (положение — по ним); вырезы и закладные — по ведомости на листе, до обшивки; отверстия не совмещать с профилями.
3. Пом. 6, 7, 8, 9, 10, 11, 12, 13 — потолок по плите без подвесной системы; отделка — по ведомости отделки.

| | | | | | |
|---|---|---|---|---|---|
| | | | | | Проект: Дом 120 м² |
| | Лист | № док. | Подпись | Дата | План потолков · 2-й этаж |
| Дизайнер | Кырлан А.С. | | | 19.10.26 | |

| Стадия | Лист | Листов |
|---|---|---|
| П | 32 | 104 |

выпуск 19.10.2026 № 46d0102a0d · стр. 32 из 104

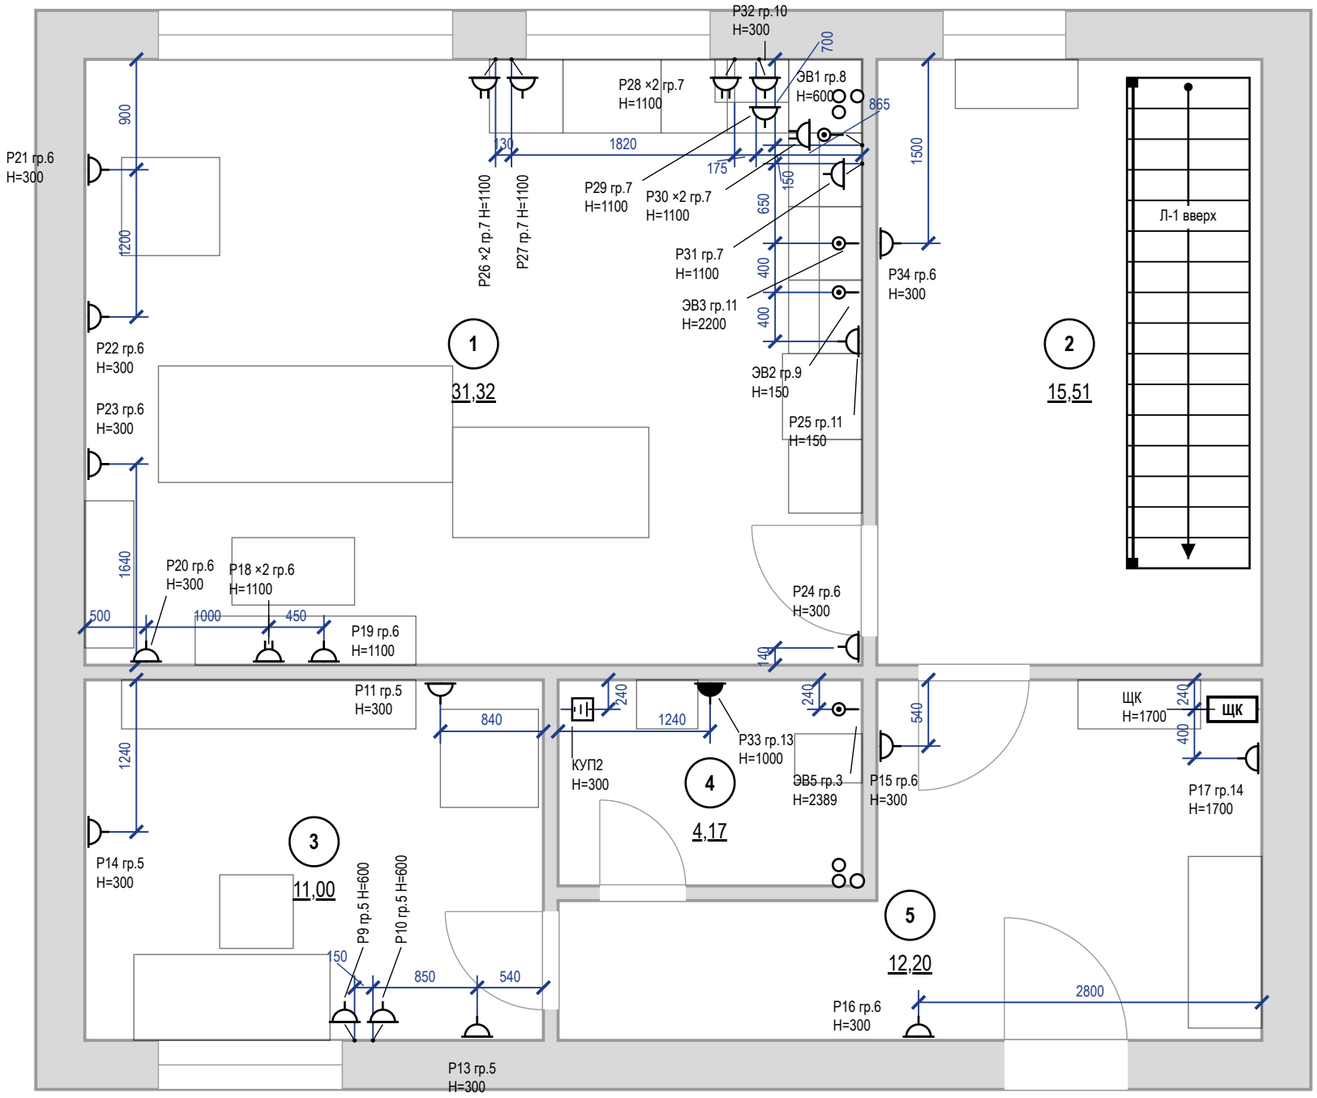


## Условные обозначения


- розетка с заземляющим контактом; у знака — марка, ×N постов в рамке, гр. — группа щита, Н — высота оси, мм
- то же, рамка на 2 поста (число черточек — число постов)
- розетка влагозащищённая IP44
- вывод кабеля для подключения прибора (без розетки), марка ЭВ
- КУП — коробка уравнивания потенциалов (ДСУП), проводник к шине РЕ щита
- ЩК — щит квартирный
- знак разведён для читаемости: точка на стене — у выноски, привязка — до неё
- мебель и сантехприборы — подложка
- стояк: К1 — канализация, В1 — ХВС, Т3 — ГВС
- 1 — номер помещения, площадь м²

## Примечания

1. За отметку 0,000 принят уровень чистого пола. Высоты Н — от чистого пола до оси изделия; привязки — от чистовой грани стены до оси механизма (у рамки на несколько постов — до оси рамки).
2. Высота установки, не указанная на плане: розетки — 300 мм от чистого пола; выводы кабеля — по паспорту прибора.
3. Розетки в санузле — только вне зон 0–2 (ПУЭ 7.1.48, ГОСТ Р 50571.7.701-2024), IP44, через УЗО 30 мА.
4. Розеточные и мокрые линии — через УЗО или дифавтомат с током утечки не более 30 мА (ПУЭ 7.1.79); в санузле выполнить ДСУП (ПУЭ 7.1.87–7.1.88).
5. Кабель — медный, исполнение нг(А)-LS (ГОСТ 31565-2012); скрытая прокладка только горизонтально и вертикально, фактические трассы зафиксировать исполнительной схемой до закрытия отделкой.
6. Расчёт нагрузок, токов КЗ, селективности и сечений — по проекту ЭОМ организации с допуском СРО; лист задаёт состав, расположение и группы.
7. Выводы кухонной техники — после утверждения проекта кухни (ориентировочно); привязки выводов даны от осей модулей гарнитура и пересматриваются вместе с проектом кухни.
8. Электрический тёплый пол проектом не предусмотрен; при решении заказчика устроить — отдельный лист «План тёплых полов»: контуры с отступом 100 мм от стен и мебели без ножек, датчик в гофре, терморегулятор, своя группа щита через УЗО 30 мА.
9. Ведомости электроточек, изделий, светильников и расшифровка клавиш — лист «Ведомость электроточек и изделий».

| | | | | | | |
|---|---|---|---|---|---|---|
| | | | | | Проект: Дом 120 м² | |
| | Лист | № док. | Подпись | Дата | План розеток и электровыводов · 1-й этаж | Стадия / Лист / Листов |
| Дизайнер | Кырлан А.С. | | | 19.10.26 | | П / 33 / 104 |

выпуск 19.10.2026 № 46d0102a0d · стр. 33 из 104

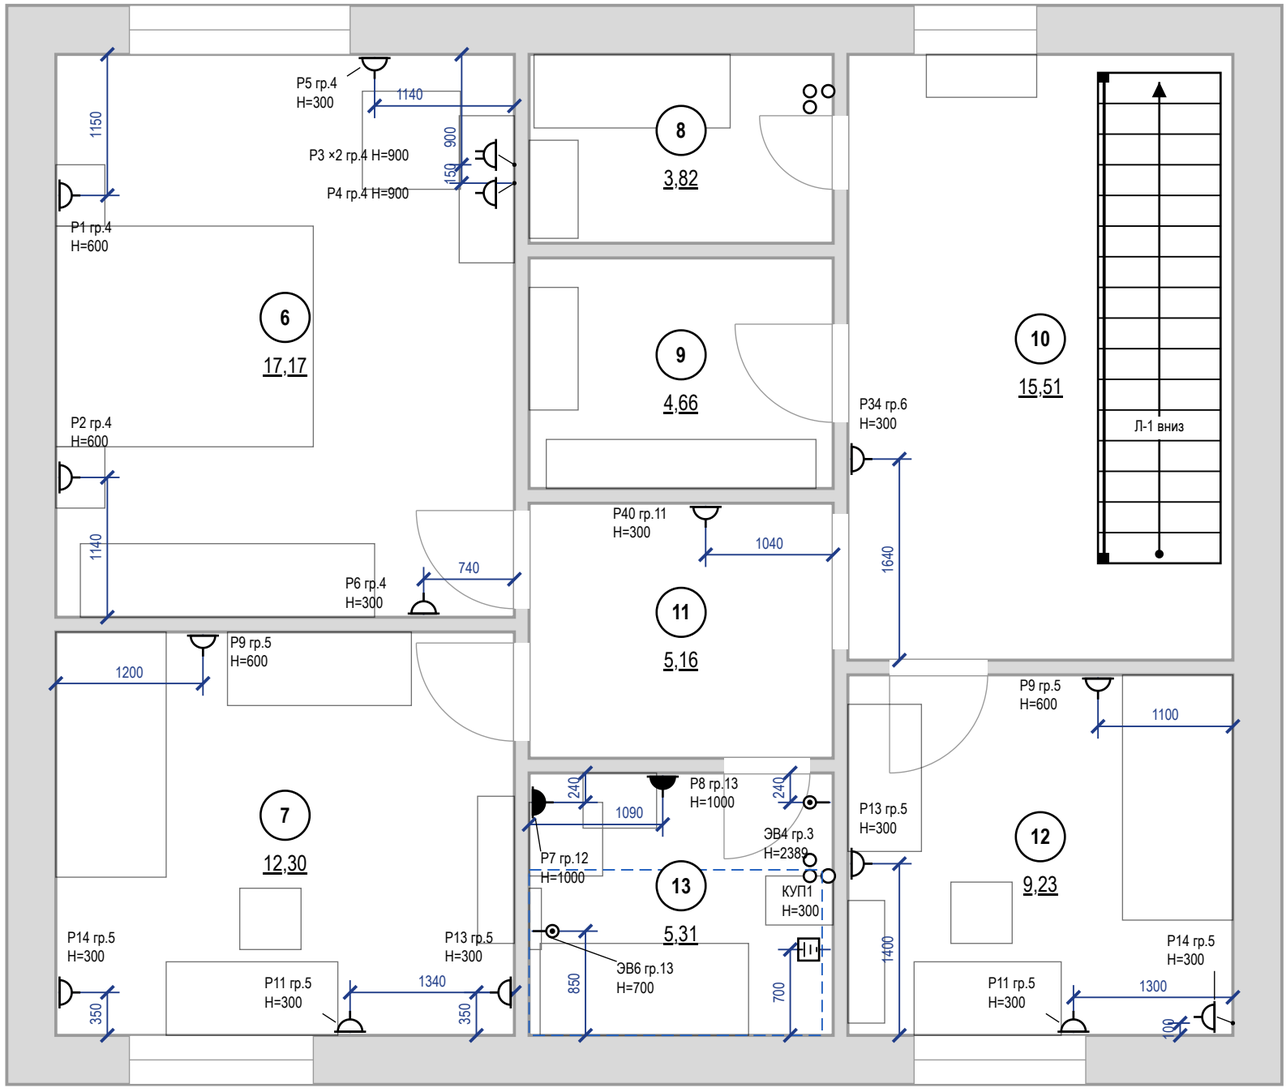


## Условные обозначения


- розетка с заземляющим контактом; у знака — марка, ×N постов в рамке, гр. — группа щита, Н — высота оси, мм
- то же, рамка на 2 поста (число черточек — число постов)
- розетка влагозащищённая IP44
- вывод кабеля для подключения прибора (без розетки), марка ЭВ
- КУП — коробка уравнивания потенциалов (ДСУП), проводник к шине РЕ щита
- знак разведён для читаемости: точка на стене — у выноски, привязка — до неё
- граница зоны 2 ванной (600 мм от ванны/поддона)
- мебель и сантехприборы — подложка
- стояк: К1 — канализация, В1 — ХВС, Т3 — ГВС
- (1) номер помещения, площадь м²

## Примечания

1. За отметку 0,000 принят уровень чистого пола. Высоты Н — от чистого пола до оси изделия; привязки — от чистовой грани стены до оси механизма (у рамки на несколько постов — до оси рамки).
2. Высота установки, не указанная на плане: розетки — 300 мм от чистого пола; выводы кабеля — по паспорту прибора.
3. Розетки в санузле — только вне зон 0–2 (ПУЭ 7.1.48, ГОСТ Р 50571.7.701-2024), IP44, через УЗО 30 мА.
4. Розеточные и мокрые линии — через УЗО или дифавтомат с током утечки не более 30 мА (ПУЭ 7.1.79); в санузле выполнить ДСУП (ПУЭ 7.1.87–7.1.88).
5. Кабель — медный, исполнение нг(А)-LS (ГОСТ 31565-2012); скрытая прокладка только горизонтально и вертикально, фактические трассы зафиксировать исполнительной схемой до закрытия отделкой.
6. Расчёт нагрузок, токов КЗ, селективности и сечений — по проекту ЭОМ организации с допуском СРО; лист задаёт состав, расположение и группы.
7. Электрический тёплый пол проектом не предусмотрен; при решении заказчика устроить — отдельный лист «План тёплых полов»: контуры с отступом 100 мм от стен и мебели без ножек, датчик в гофре, терморегулятор, своя группа щита через УЗО 30 мА.
8. Ведомости электроточек, изделий, светильников и расшифровка клавиш — лист «Ведомость электроточек и изделий».

| | | | | | | | |
|---|---|---|---|---|---|---|---|
| | | | | | Проект: Дом 120 м² | | |
| | Лист | № док. | Подпись | Дата | План розеток и электровыводов · 2-й этаж | Стадия | Лист | Листов |
| Дизайнер | Кырлан А.С. | | | 19.10.26 | | П | 34 | 104 |

выпуск 19.10.2026 № 46d0102a0d · стр. 34 из 104

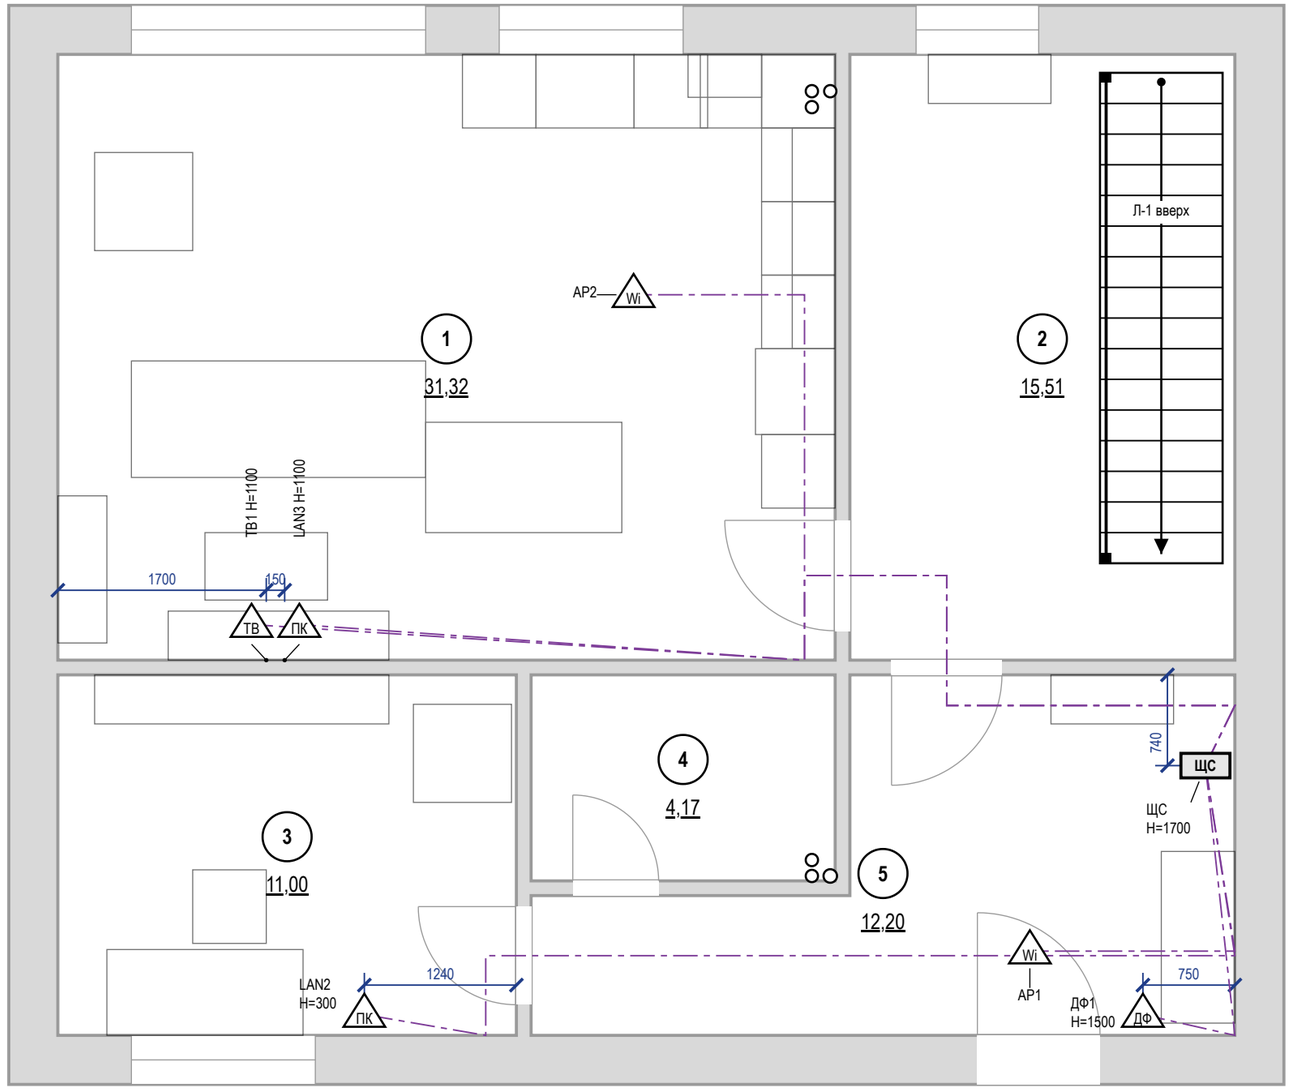



## Примечания

1. За отметку 0,000 принят уровень чистого пола. Высоты H — от чистого пола до оси изделия; привязки — от чистовой грани стены до оси механизма (у рамки на несколько постов — до оси рамки).
2. Высота установки, не указанная на плане: розетки LAN и ТВ — 300 мм от чистого пола.
3. Слаботочные кабели — отдельно от силовых: в своей трубе или лотке, при параллельной прокладке не ближе 100 мм к силовым, пересечения под прямым углом; каждую точку — отдельным кабелем от ЩС без скруток.
4. Трассы на листе — принципиальные; фактические зафиксировать исполнительной схемой до закрытия отделкой. Силовые линии, УЗО 30 мА, ДСУП, кабель нг(A)-LS — по листам розеток и щита.
5. Проект силовой части и расчёт токов КЗ — по проекту ЭОМ; слаботочная часть согласуется с провайдером и управляющей компанией (домофон, коллективное ТВ).

| | | | | | | |
|---|---|---|---|---|---|---|
| | | | | | Проект: Дом 120 м² | |
| | Лист | № док. | Подпись | Дата | | |
| Дизайнер | Кырлан А.С. | | | 19.10.26 | План слаботочных сетей · 1-й этаж | Стадия: П; Лист: 35; Листов: 104 |

выпуск 19.10.2026 № 46d0102a0d · стр. 35 из 104

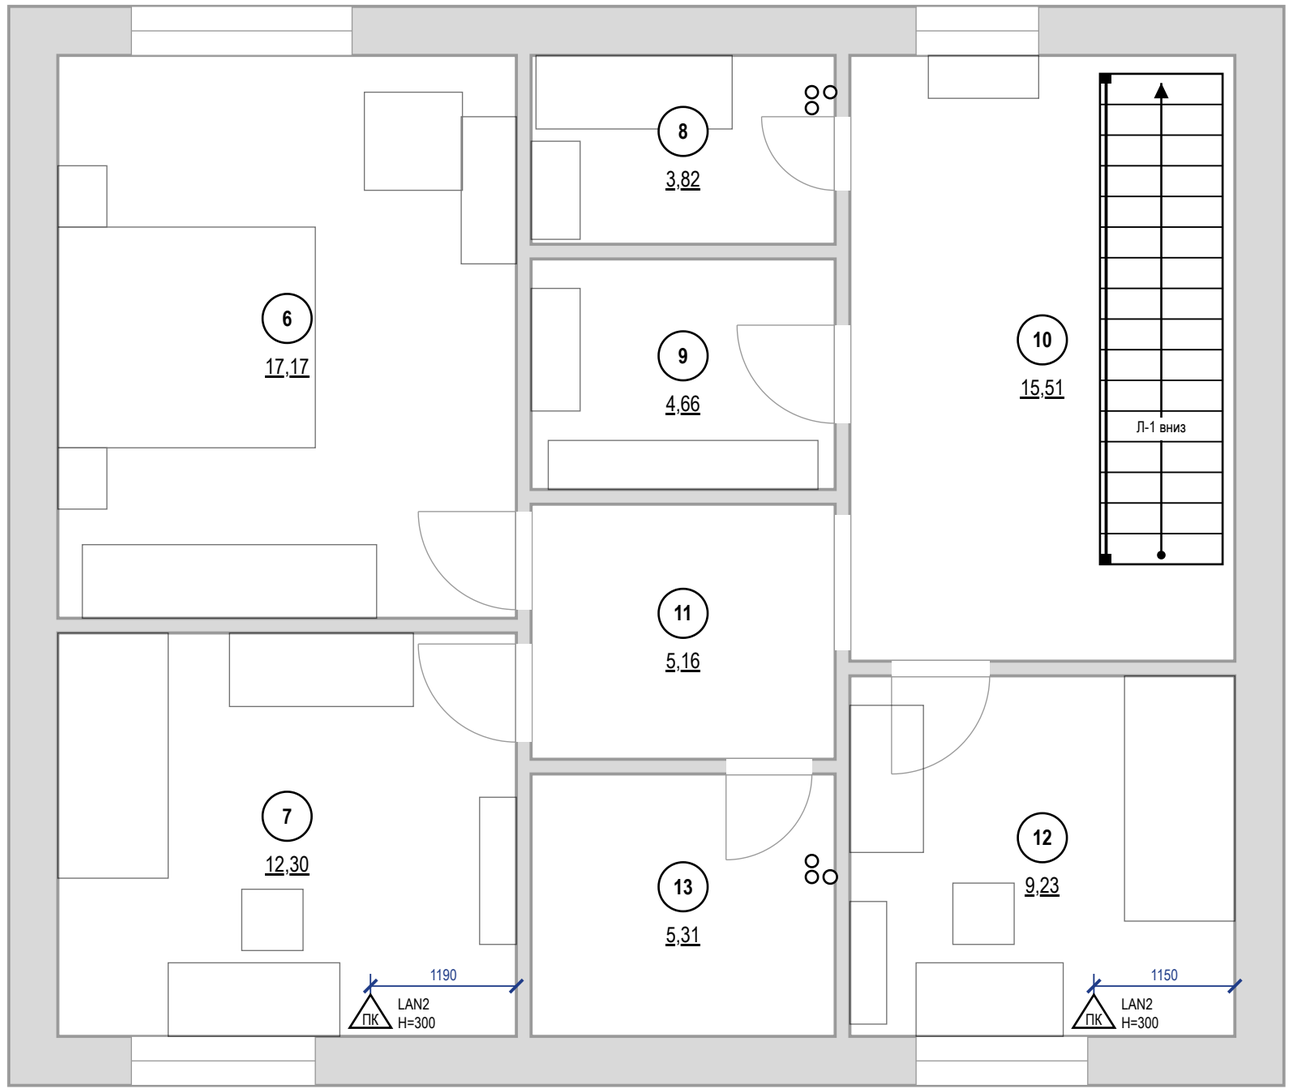



## Примечания

1. За отметку 0,000 принят уровень чистого пола. Высоты H — от чистого пола до оси изделия; привязки — от чистовой грани стены до оси механизма (у рамки на несколько постов — до оси рамки).
2. Высота установки, не указанная на плане: розетки LAN и ТВ — 300 мм от чистого пола.
3. Слаботочные кабели — отдельно от силовых: в своей трубе или лотке, при параллельной прокладке не ближе 100 мм к силовым, пересечения под прямым углом; каждую точку — отдельным кабелем от ЩС без скруток.
4. Трассы на листе — принципиальные; фактические зафиксировать исполнительной схемой до закрытия отделкой. Силовые линии, УЗО 30 мА, ДСУП, кабель нг(A)-LS — по листам розеток и щита.
5. Проект силовой части и расчёт токов КЗ — по проекту ЭОМ; слаботочная часть согласуется с провайдером и управляющей компанией (домофон, коллективное ТВ).

| | | | | | |
|---|---|---|---|---|---|
| | | | | | Проект: Дом 120 м² |
| | Лист | № док. | Подпись | Дата | |
| Дизайнер | Кырлан А.С. | | | 19.10.26 | План слаботочных сетей · 2-й этаж |

| Стадия | Лист | Листов |
|---|---|---|
| П | 36 | 104 |

выпуск 19.10.2026 № 46d0102a0d · стр. 36 из 104

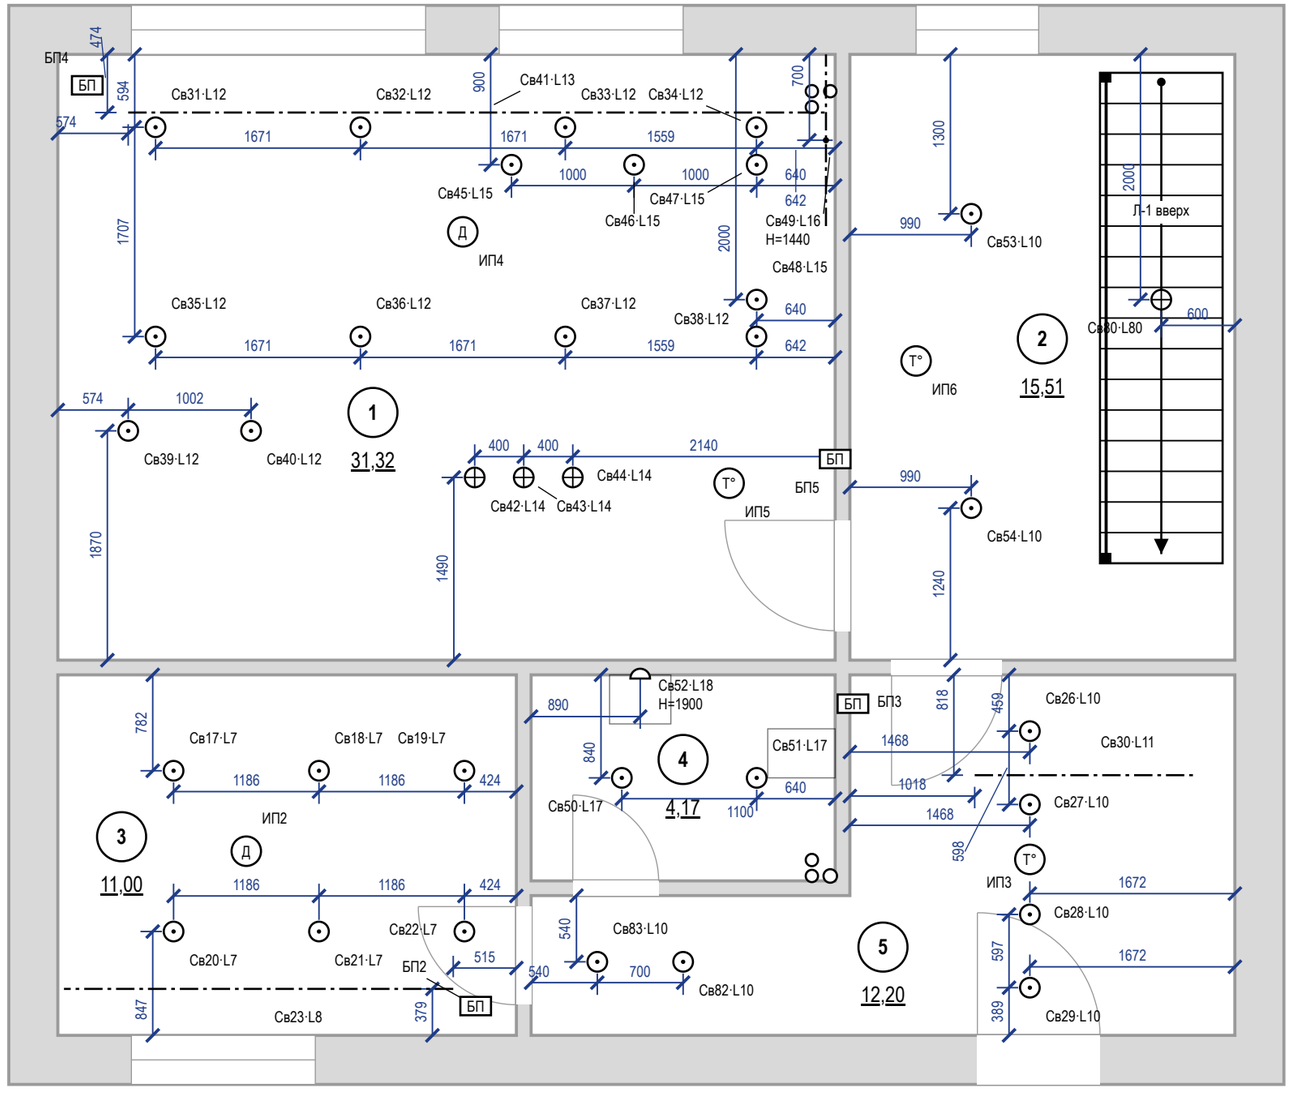



## Примечания

1. За отметку 0,000 принят уровень чистого пола. Высоты H — от чистого пола до оси изделия; привязки — от чистовой грани стены до оси механизма (у рамки на несколько постов — до оси рамки).
2. Высота установки, не указанная на плане: светильники — на потолке; настенные — по отметке H у знака. Привязки — до оси светильника от чистовой грани стены, по рядам.
3. Освещённость: Eн — СанПиН 1.2.3685-21, табл. 5.52 (на полу); Ф треб. = Eн·S/(U·MF) при U = 0,5 и MF = 0,71 (СП 52.13330.2016, табл. 4.3) — оценка, не светотехнический расчёт. Декоративная подсветка в Ф не входит.
4. Во влажных помещениях — светильники не ниже IP44; в зонах 0–2 ванной — по ГОСТ Р 50571.7.701-2024 (зона 1 — IPX5).
5. Розеточные и мокрые линии — через УЗО или дифавтомат с током утечки не более 30 мА (ПУЭ 7.1.79); в санузле выполнить ДСУП (ПУЭ 7.1.87–7.1.88).
6. Кабель — медный, исполнение нг(A)-LS (ГОСТ 31565-2012); скрытая прокладка только горизонтально и вертикально, фактические трассы зафиксировать исполнительной схемой до закрытия отделкой.
7. Расчёт нагрузок, токов КЗ, селективности и сечений — по проекту ЭОМ организации с допуском СРО; лист задаёт состав, расположение и группы.
8. Ведомость светильников — лист «Ведомость электроточек и изделий».

| | | | | | |
|---|---|---|---|---|---|
| | | | | | Проект: Дом 120 м² |
| | Лист | № док. | Подпись | Дата | План освещения · 1-й этаж |
| Дизайнер | Кырлан А.С. | | | 19.10.26 | |

| Стадия | Лист | Листов |
|---|---|---|
| П | 37 | 104 |

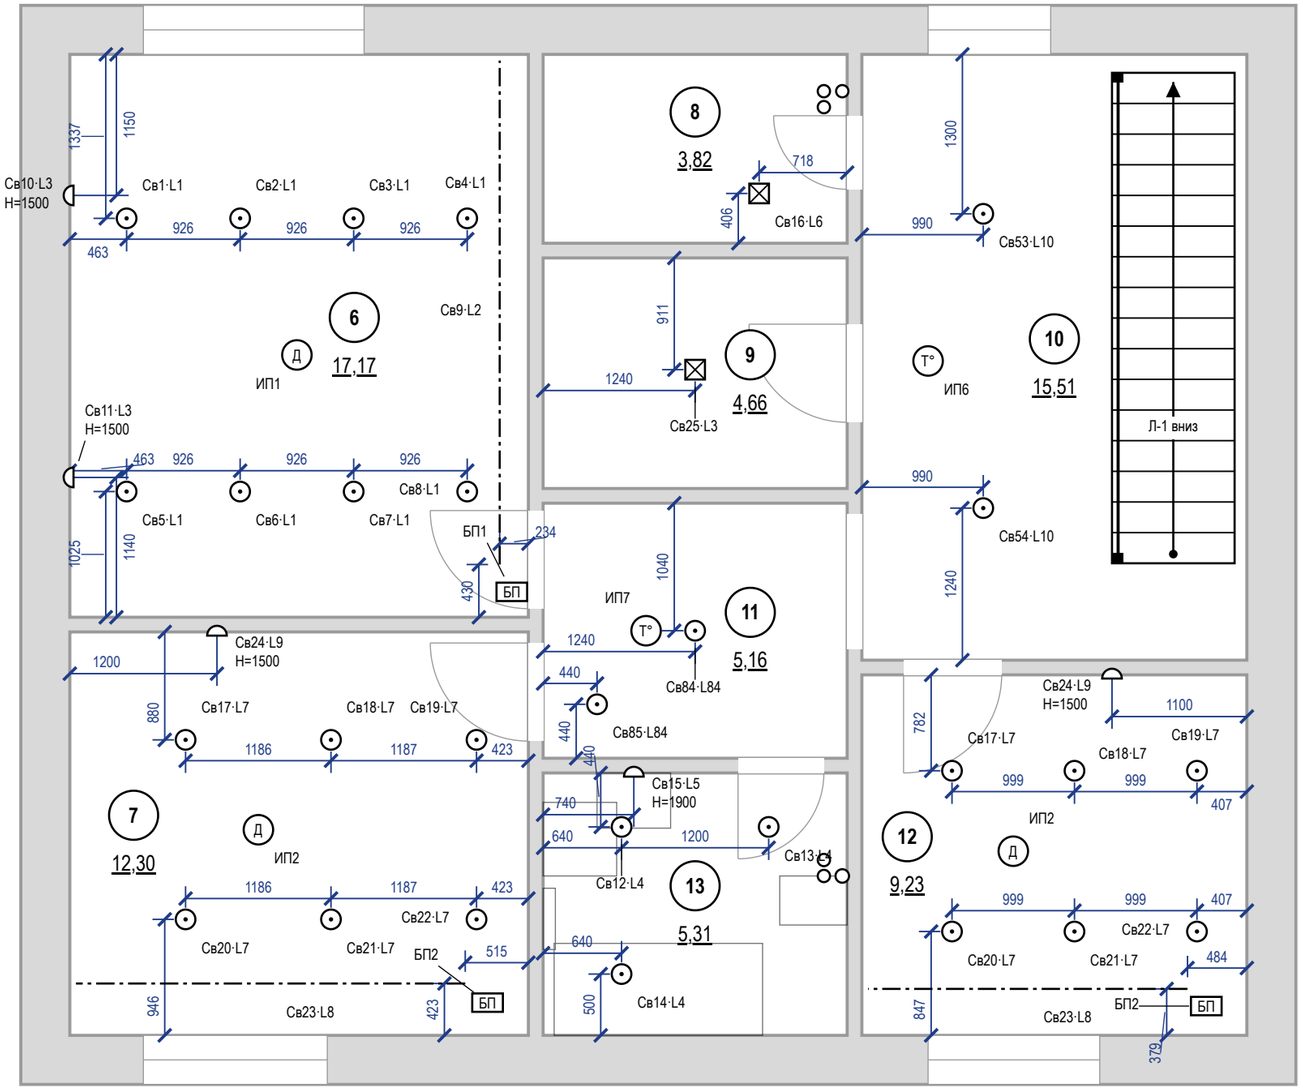


## Примечания

1. За отметку 0,000 принят уровень чистого пола. Высоты Н — от чистого пола до оси изделия; привязки — от чистовой грани стены до оси механизма (у рамки на несколько постов — до оси рамки).
2. Высота установки, не указанная на плане: светильники — на потолке; настенные — по отметке Н у знака. Привязки — до оси светильника от чистовой грани стены, по рядам.
3. Освещённость: Ен — СанПиН 1.2.3685-21, табл. 5.52 (на полу); Ф треб. = Ен·S/(U·MF) при U = 0,5 и MF = 0,71 (СП 52.13330.2016, табл. 4.3) — оценка, не светотехнический расчёт. Декоративная подсветка в Ф не входит.
4. Во влажных помещениях — светильники не ниже IP44; в зонах 0–2 ванной — по ГОСТ Р 50571.7.701-2024 (зона 1 — IPX5).
5. Розеточные и мокрые линии — через УЗО или дифавтомат с током утечки не более 30 мА (ПУЭ 7.1.79); в санузле выполнить ДСУП (ПУЭ 7.1.87–7.1.88).
6. Кабель — медный, исполнение нг(A)-LS (ГОСТ 31565-2012); скрытая прокладка только горизонтально и вертикально, фактические трассы зафиксировать исполнительной схемой до закрытия отделкой.
7. Расчёт нагрузок, токов КЗ, селективности и сечений — по проекту ЭОМ организации с допуском СРО; лист задаёт состав, расположение и группы.
8. Ведомость светильников — лист «Ведомость электроточек и изделий».

| | | | | | |
|---|---|---|---|---|---|
| | | | | | Проект: Дом 120 м² |
| | Лист | № док. | Подпись | Дата | План освещения · 2-й этаж |
| Дизайнер | Кырлан А.С. | | | 19.10.26 | |

| Стадия | Лист | Листов |
|---|---|---|
| П | 38 | 104 |

выпуск 19.10.2026 № 46d0102a0d · стр. 38 из 104

## Спецификация светильников

| Поз. | Марки | Наименование | Установка | Кол. | P, Вт | Σ P, Вт | Ф, лм | Тц, К | Ra | Угол, ° | IP | Дим. | Группа | Пом. |
|---|---|---|---|---|---|---|---|---|---|---|---|---|---|---|
| 1 | Св31–Св40 | Встраиваемый точечный | встраиваемый | 10 | 12 | 120 | 1000 | 3000 | 90 | — | 20 | да | L12 | 1 |
| 2 | Св41 | Лента светодиодная 24 В | в коробе, профиль с рассеивателем | 22,1 м | 9,6/м | 212,2 | 900/м | 2700 | 90 | — | 20 | да | L13 | 1 |
| 3 | Св42, Св43, Св44 | Подвесной | подвес, низ H=1450 | 3 | 9 | 27 | 800 | 3000 | 90 | — | 20 | да | L14 | 1 |
| 4 | Св45–Св48 | Встраиваемый точечный | встраиваемый | 4 | 10 | 40 | 900 | 3000 | 90 | — | 20 | да | L15 | 1 |
| 5 | Св49 | Линейный настенный | под верхними шкафами, H=1440 | 1 | 18 | 18 | 1500 | 3000 | 90 | — | 20 | да | L16 | 1 |
| 6 | Св26–Св29, Св53, Св54, Св82–Св85 | Встраиваемый точечный | встраиваемый | 12 | 7 | 84 | 600 | 3000 | 90 | — | 20 | — | L10, L84 | 2, 5, 10, 11 |
| 7 | Св80 | Подвесной | подвес | 1 | 12 | 12 | 1100 | 3000 | 90 | — | 20 | — | L80 | 2 |
| 8 | Св17–Св22 | Встраиваемый точечный | встраиваемый | 6 | 14 | 84 | 1400 | 2700 | 90 | — | 20 | — | L7 | 3 |
| 9 | Св23 | Лента светодиодная 24 В | в коробе, профиль с рассеивателем | 12,3 м | 9,6/м | 118,1 | 900/м | 2700 | 90 | — | 20 | да | L8 | 3 |
| 10 | Св50 | Встраиваемый точечный | встраиваемый | 1 | 7 | 7 | 600 | 3000 | 90 | — | 44 | — | L17 | 4 |
| 11 | Св12–Св14, Св51 | Встраиваемый точечный | встраиваемый | 4 | 6 | 24 | 500 | 3000 | 90 | — | 44 | — | L4, L17 | 4, 13 |
| 12 | Св15, Св52 | Настенный светильник над зеркалом, драйвер встроен | над зеркалом, H=1900 | 2 | 8 | 16 | 600 | 3000 | 90 | — | 44 | — | L5, L18 | 4, 13 |
| 13 | Св30 | Лента светодиодная 24 В | в коробе, профиль с рассеивателем, датчик движения | 1,8 м | 4,8/м | 8,6 | 150/м | 2700 | 90 | — | 20 | нет | L11 | 5 |
| 14 | Св1–Св8 | Встраиваемый точечный | встраиваемый | 8 | 12 | 96 | 1000 | 2700 | 90 | — | 20 | — | L1 | 6 |
| 15 | Св9 | Лента светодиодная 24 В | в коробе, профиль с рассеивателем | 15,5 м | 9,6/м | 148,8 | 900/м | 2700 | 90 | — | 20 | да | L2 | 6 |
| 16 | Св10, Св11, Св24 | Настенный (бра) | на стене, H=1500 | 4 | 6 | 24 | 400 | 2700 | 90 | 60 | 20 | — | L3, L9 | 6, 7, 12 |
| 17 | Св17–Св22 | Встраиваемый точечный | встраиваемый | 12 | 11 | 132 | 1100 | 2700 | 90 | — | 20 | — | L7 | 7, 12 |
| 18 | Св23 | Лента светодиодная 24 В | в коробе, профиль с рассеивателем | 24,6 м | 9,6/м | 236,2 | 900/м | 2700 | 90 | — | 20 | да | L8 | 7, 12 |
| 19 | Св16 | Потолочный накладной | на потолке, засветка стены | 1 | 10 | 10 | 900 | 3000 | 90 | — | 20 | — | L6 | 8 |
| 20 | Св25 | Потолочный накладной | на потолке | 1 | 9 | 9 | 600 | 3000 | 90 | — | 20 | — | L3 | 9 |
| | | **Итого** | | **70 шт + 76,3 м** | | **1426,8** | | | | | | | | |

## LED-ленты, линейные светильники и блоки питания

| Марка | Пом. | L, м | U, В | Вт/м | Σ P, Вт | БП | P БП, Вт | Загр., % | Питание | Доступ к БП |
|---|---|---|---|---|---|---|---|---|---|---|
| Св41 | 1 | 22,1 | 24 | 9,6 | 212,2 | БП4 | 300 | 71 | с двух концов | люк 300×300 в коробе У1 у входа |
| Св49 | 1 | 3 | 24 | — | 18 | БП5 | 60 | 30 | встроенный ввод | в пенале M_32, верх, съёмная панель |
| Св23 | 3 | 12,3 | 24 | 9,6 | 118,1 | БП2 | 200 | 177 | с двух концов | люк 300×300 в коробе У1 у окна |
| Св30 | 5 | 1,8 | 24 | 4,8 | 8,6 | БП3 | 20 | 43 | с одного конца | в шкафу M16, верхняя полка |
| Св9 | 6 | 15,5 | 24 | 9,6 | 148,8 | БП1 | 200 | 74 | с двух концов | люк 300×300 в коробе У1 у входа |
| Св23 | 7 | 12,3 | 24 | 9,6 | 118,1 | БП2 | 200 | 177 | с двух концов | люк 300×300 в коробе У1 у окна |
| Св23 | 12 | 12,3 | 24 | 9,6 | 118,1 | БП2 | 200 | 177 | с двух концов | люк 300×300 в коробе У1 у окна |

## Сценарии освещения

| Пом. | Сценарий | Группы и уровни, % | Чем включается |
|---|---|---|---|
| 1 | Вечер | L12 споты гостиной — 30; L13 подсветка короба — 100; L14 подвесы над столом — 50; L15 споты кухни — 0; L16 подсветка столешницы — 0 | S10 светорегулятор, S11 светорегулятор |
| 1 | Ужин | L12 споты гостиной — 0; L13 подсветка короба — 60; L14 подвесы над столом — 100; L15 споты кухни — 0; L16 подсветка столешницы — 30 | S10 светорегулятор, S11 светорегулятор, S12 светорегулятор |
| 1 | Кино | L12 споты гостиной — 0; L13 подсветка короба — 20; L14 подвесы над столом — 0; L15 споты кухни — 0; L16 подсветка столешницы — 0 | S10 светорегулятор |
| 1 | Готовка | L12 споты гостиной — 50; L13 подсветка короба — 0; L14 подвесы над столом — 0; L15 споты кухни — 100; L16 подсветка столешницы — 100 | S10 светорегулятор, S11 светорегулятор, S12 светорегулятор |
| 3 | Вечер | L7 споты — 0; L8 подсветка короба — 100; L9 бра — 100 | S4, S5 |
| 6 | Вечер | L1 споты — 0; L2 подсветка короба — 100; L3 бра — 100 | S1, S2, S3 |
| 6 | Уборка | L1 споты — 100; L2 подсветка короба — 100; L3 бра — 0 | S1, S2, S3 |
| 7 | Вечер | L7 споты — 0; L8 подсветка короба — 100; L9 бра — 100 | S4, S5 |
| 12 | Вечер | L7 споты — 0; L8 подсветка короба — 100; L9 бра — 100 | S4, S5 |

## Слои света

общий — равномерный свет помещения, по норме освещённости

рабочий — местный свет задачи: столешница, зеркало, чтение у кровати


акцентный — подсветка потолка, стен и ниш; не входит в поток общего света

ночной — путь спальня → санузел: не выше 2700 K, малая яркость, датчик движения

## Примечания

1. Позиции и марки Св — те же, что на плане освещения (лист «План освещения») и в ведомости светильников (лист «Ведомость электроточек и изделий»); группы L — по плану выключателей (лист «План выключателей»).
2. Модели светильников не назначены: подбор по графам спецификации — поток, Тц, Ra, угол, IP и диммирование не хуже указанных, мощность не больше. IP 20 — сухие помещения.
3. Длина LED-ленты в карнизе — по линии карниза плана потолков (лист «План потолков»); Σ P = Вт/м × длина. Блок питания загружен не больше чем на 80 %; лента 24 В длиннее 10 м питается с двух концов; доступ к блоку питания — люк ревизии 300×300 мм или место, указанное в таблице.
4. Сценарии: уровень — доля максимальной яркости группы, %; 0 — группа выключена. Уровень ниже 100 % — только у групп на светорегуляторе (задний фронт, TE) с диммируемыми драйверами и блоками питания.
5. Мощность и поток — по паспортам принятых изделий, Σ P — установленная мощность освещения. Оценка освещённости — на плане освещения; это не светотехнический расчёт.
6. Не поместилось строк таблиц: 13 — продолжение выпустить отдельным листом.


| | | | | | Проект: Дом 120 м² | | | |
|---|---|---|---|---|---|---|---|---|
| | Лист | № док. | Подпись | Дата | Спецификация светильников и сценарии освещения | Стадия | Лист | Листов |
| Дизайнер | Кырлан А.С. | | | 19.10.26 | | П | 39 | 104 |

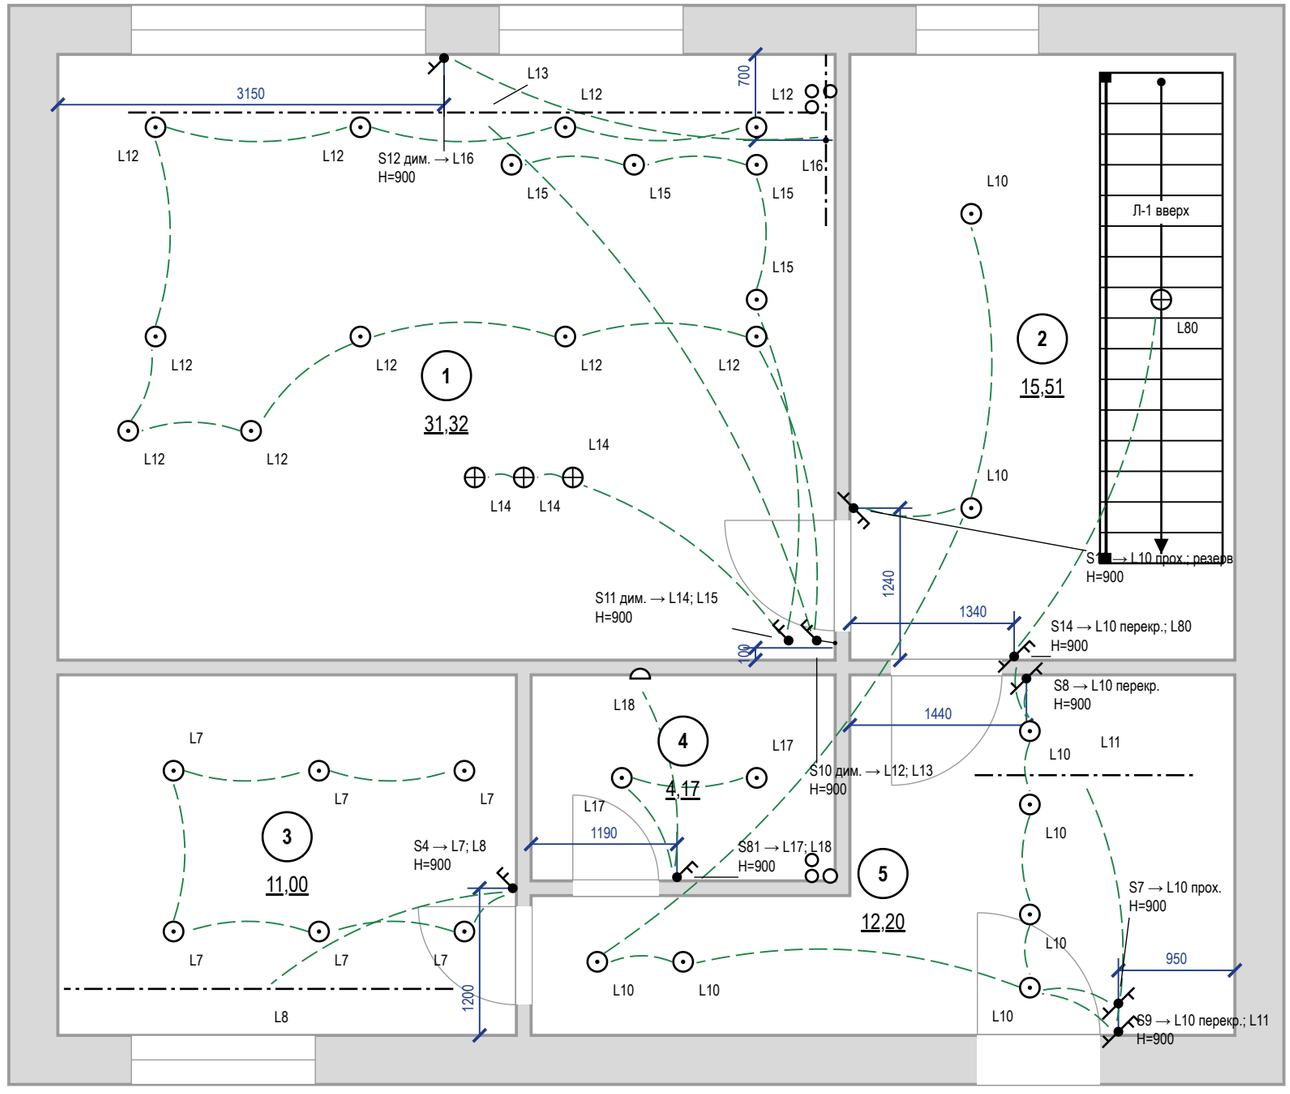


## Примечания

1. За отметку 0,000 принят уровень чистого пола. Высоты H — от чистого пола до оси изделия; привязки — от чистовой грани стены до оси механизма (у рамки на несколько постов — до оси рамки).
2. Высота установки, не указанная на плане: выключатели — 900 мм от чистого пола, со стороны дверной ручки (ПУЭ 7.1.51).
3. Линии связи показывают, какой выключатель какую группу L включает; это не трасса кабеля. Трасса — принципиальная, фактическую зафиксировать исполнительной схемой.
4. Группы из нескольких мест (L10 — S7, S8, S9, S14, S16): на крайних местах — проходные клавиши, на промежуточных — перекрёстные; механизмы — в ведомости изделий.
5. Светорегулятор — по заднему фронту (для LED-драйверов), совместимость с драйверами проверить до закупки.
6. Розеточные и мокрые линии — через УЗО или дифавтомат с током утечки не более 30 мА (ПУЭ 7.1.79); в санузле выполнить ДСУП (ПУЭ 7.1.87–7.1.88).
7. Кабель — медный, исполнение нг(A)-LS (ГОСТ 31565-2012); скрытая прокладка только горизонтально и вертикально, фактические трассы зафиксировать исполнительной схемой до закрытия отделкой.
8. Расчёт нагрузок, токов КЗ, селективности и сечений — по проекту ЭОМ организации с допуском СРО; лист задаёт состав, расположение и группы.
9. Расшифровка клавиш и ведомость изделий — лист «Ведомость электроточек и изделий».

| | | | | | Проект: Дом 120 м² | | | |
|---|---|---|---|---|---|---|---|---|
| | Лист | № док. | Подпись | Дата | Управление светильниками · 1-й этаж | Стадия | Лист | Листов |
| Дизайнер | Кырлан А.С. | | | 19.10.26 | | П | 40 | 104 |

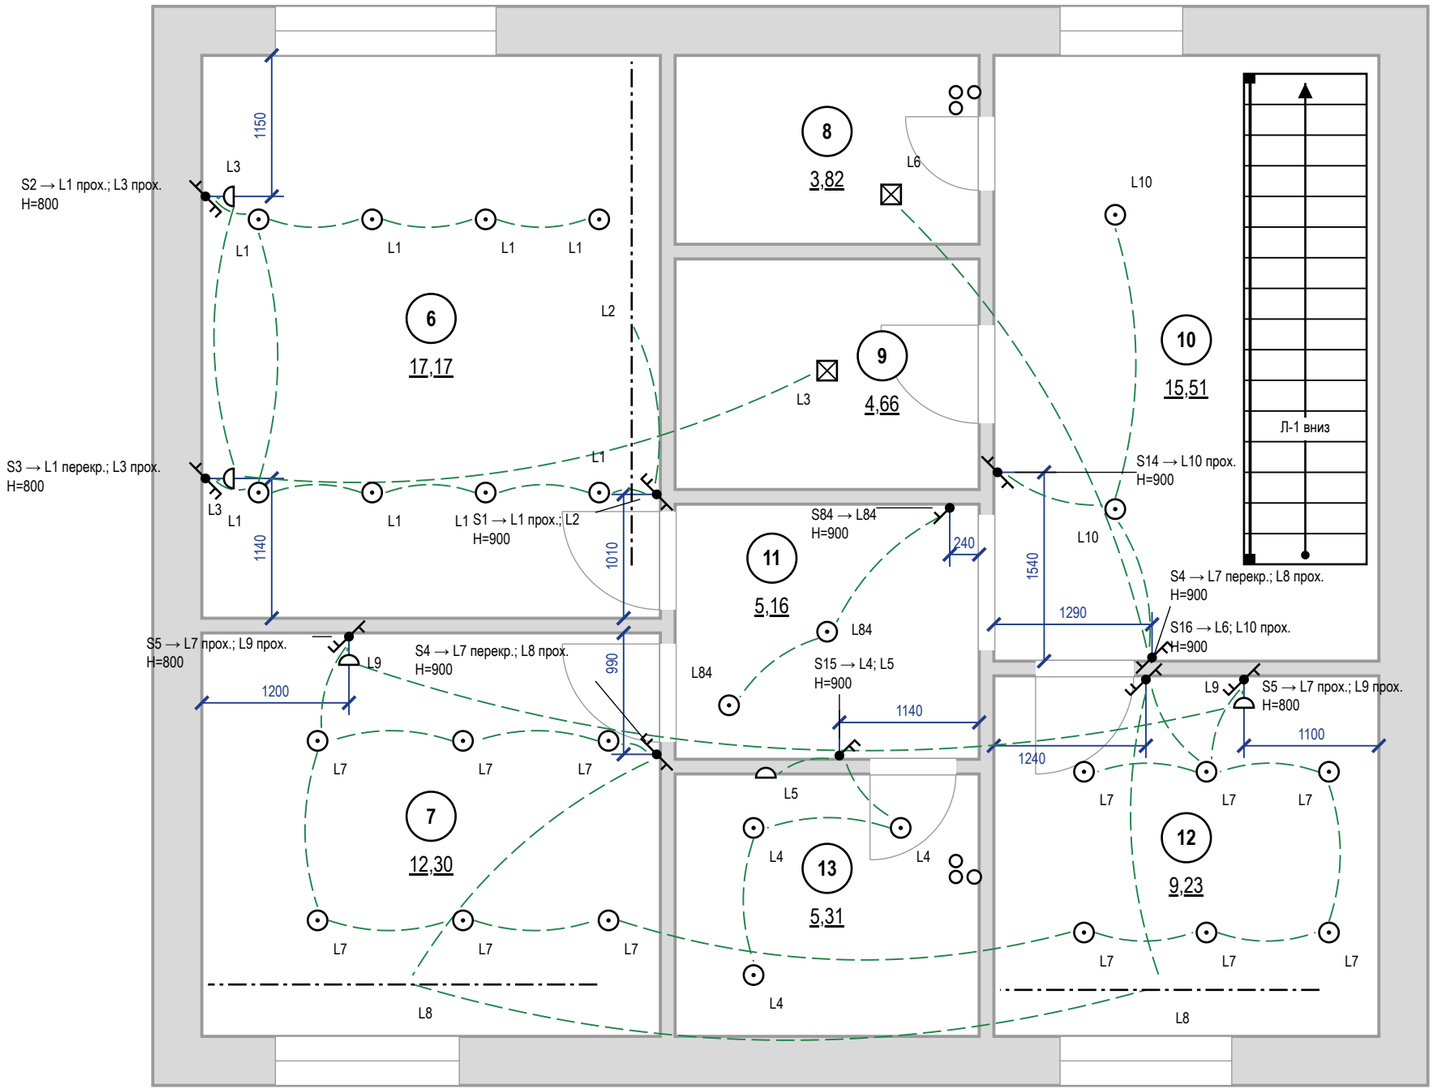



## Примечания

1. За отметку 0,000 принят уровень чистого пола. Высоты H — от чистого пола до оси изделия; привязки — от чистовой грани стены до оси механизма (у рамки на несколько постов — до оси рамки).
2. Высота установки, не указанная на плане: выключатели — 900 мм от чистого пола, со стороны дверной ручки (ПУЭ 7.1.51).
3. Линии связи показывают, какой выключатель какую группу L включает; это не трасса кабеля. Трасса — принципиальная, фактическую зафиксировать исполнительной схемой.
4. Группы из нескольких мест (L1 — S1, S2, S3; L3 — S2, S3; L7 — S4, S4, S5, S5; L8 — S4, S4; L9 — S5, S5; L10 — S14, S16): на крайних местах — проходные клавиши, на промежуточных — перекрёстные; механизмы — в ведомости изделий.
5. Розеточные и мокрые линии — через УЗО или дифавтомат с током утечки не более 30 мА (ПУЭ 7.1.79); в санузле выполнить ДСУП (ПУЭ 7.1.87–7.1.88).
6. Кабель — медный, исполнение нг(A)-LS (ГОСТ 31565-2012); скрытая прокладка только горизонтально и вертикально, фактические трассы зафиксировать исполнительной схемой до закрытия отделкой.
7. Расчёт нагрузок, токов КЗ, селективности и сечений — по проекту ЭОМ организации с допуском СРО; лист задаёт состав, расположение и группы.
8. Расшифровка клавиш и ведомость изделий — лист «Ведомость электроточек и изделий».

| | | | | | |
|---|---|---|---|---|---|
| | | | | | Проект: Дом 120 м² |
| | Лист | № док. | Подпись | Дата | Управление светильниками · 2-й этаж |
| Дизайнер | Кырлан А.С. | | | 19.10.26 | |

| Стадия | Лист | Листов |
|---|---|---|
| П | 41 | 104 |

выпуск 19.10.2026 № 46d0102a0d · стр. 41 из 104

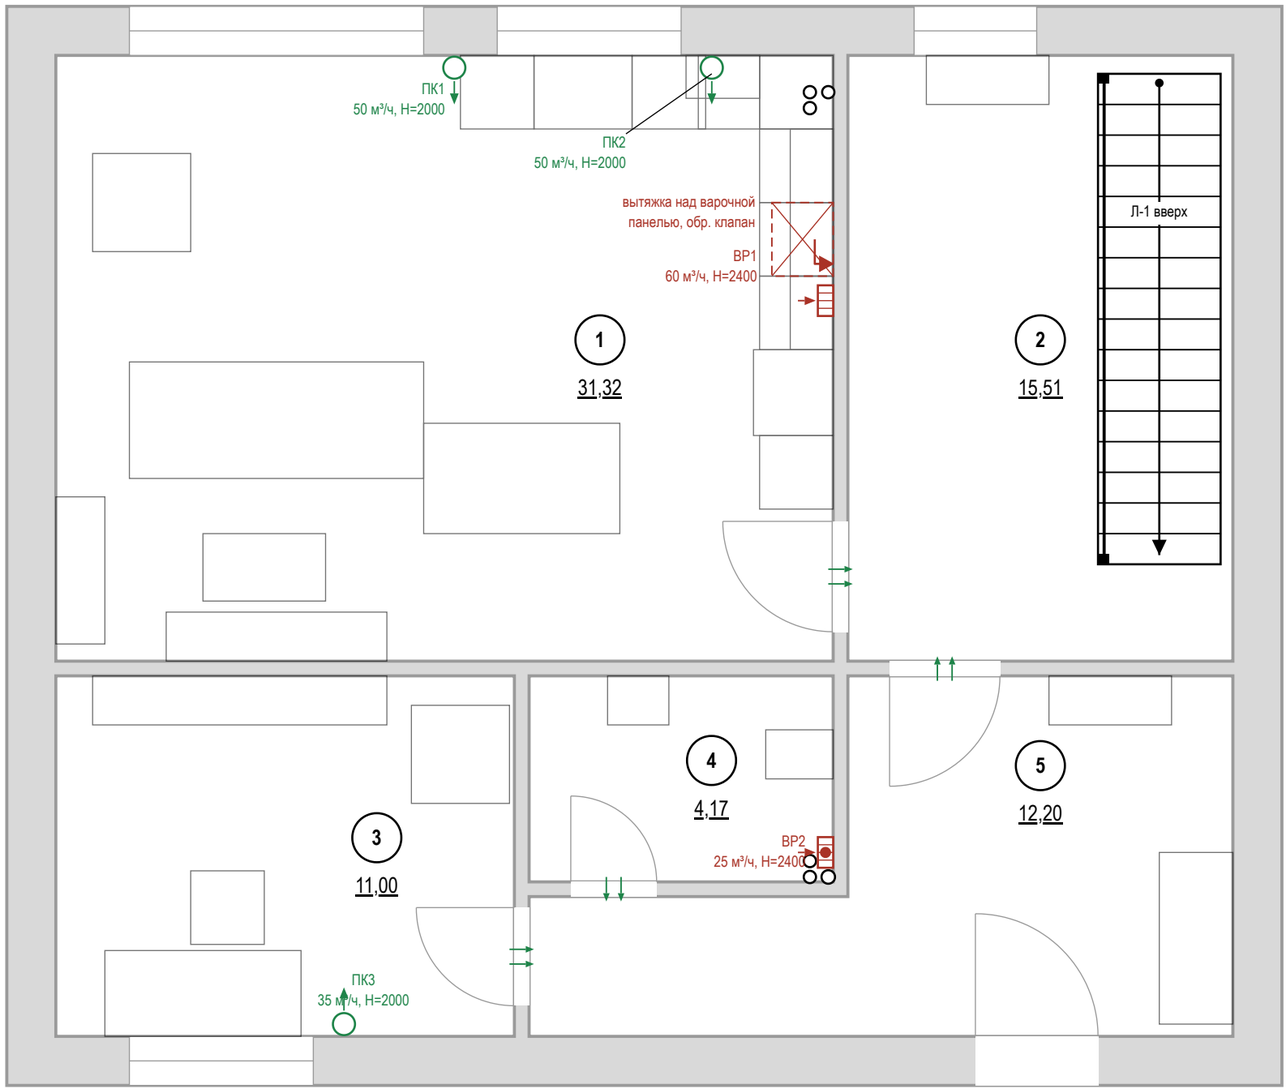


## Условные обозначения

- стояк: К1 — канализация, В1 — ХВС, Т3 — ГВС
- номер помещения, площадь м²
- вытяжная решётка в вентканал: марка, расход м³/ч, Н центра от чистого пола
- вытяжная решётка с бытовым вентилятором и обратным клапаном: марка, расход, Н
- приточный клапан (КИВ) в наружной стене: марка, расход, Н центра
- переток: зазор под полотном или переточная решётка
- кухонная вытяжка над варочной панелью
- воздуховод кухонной вытяжки в коробе под потолком
- отдельный вход воздуховода в вентканал, обратный клапан

## Воздухообмен, м³/ч

| № | Помещение | Выт. норма | Выт. проект | Прит. норма | Прит. проект | Устройства |
|---|---|---|---|---|---|---|
| 1 | Гостиная-кухня | 60 | 60 | 94 | 100 | ВР1, ПК1, ПК2 |
| 3 | Кабинет | | | 33 | 35 | ПК3 |
| 4 | Санузел гостевой | 25 | 25 | | | ВР2 |
| | **Итого** | **85** | **85** | **120** | **135** | |

Воздухообмен квартиры — по большей из сумм притока и вытяжки: норма 120 м³/ч, проект 135 м³/ч.
**Приток больше вытяжки на 50 м³/ч — поднять вытяжку.**


## Примечания

1. Расчёт систем ОВ и подбор оборудования — проектная организация с допуском СРО; лист даёт места, трассы и привязки.
2. Нормы вытяжки — СП 54.13330.2022 (Изм. 1, 2), табл. 7.1: кухня с электроплитой 60 м³/ч, с газовой 100; ванная и совмещённый санузел 50; уборная 25; гардеробная 0,2 ч⁻¹. Приток в жилые — 3 м³/ч на 1 м² (менее 20 м² общей площади на человека), иначе 30 м³/ч на человека.
3. Венткanалы и шахты не сужать, не переносить и не закрывать; вентилятор и кухонная вытяжка — через обратный клапан, без перекрытия естественной тяги.
4. Проектные расходы — не ниже нормы, вытяжка сведена с притоком вентиляторами мокрых помещений. Клапаны — в простенке у окна, центр 2000 мм, не над кроватью, не ближе 300 мм к стоякам отопления; типоразмер — на расход.
5. Кухонная вытяжка в воздухообмен не включена: воздуховод не менее Ø125 в коробе, вход в канал отдельный.
6. Переток — зазор под полотнами межкомнатных дверей или переточная решётка.
7. Кондиционирование заданием не предусмотрено; при установке трассы фреона и дренажа (не менее 40 мм/м, в К1 через сифон) и питание заложить до черновых работ.
8. Привязки оборудования — по паспортам приобретённых моделей, до черновых работ.

| | | | | | |
|---|---|---|---|---|---|
| | | | | | Проект: Дом 120 м² |
| | Лист | № док. | Подпись | Дата | План вентиляции · 1-й этаж |
| Дизайнер | Кырлан А.С. | | | 19.10.26 | |

| Стадия | Лист | Листов |
|---|---|---|
| П | 42 | 104 |

выпуск 19.10.2026 № 46d0102a0d · стр. 42 из 104

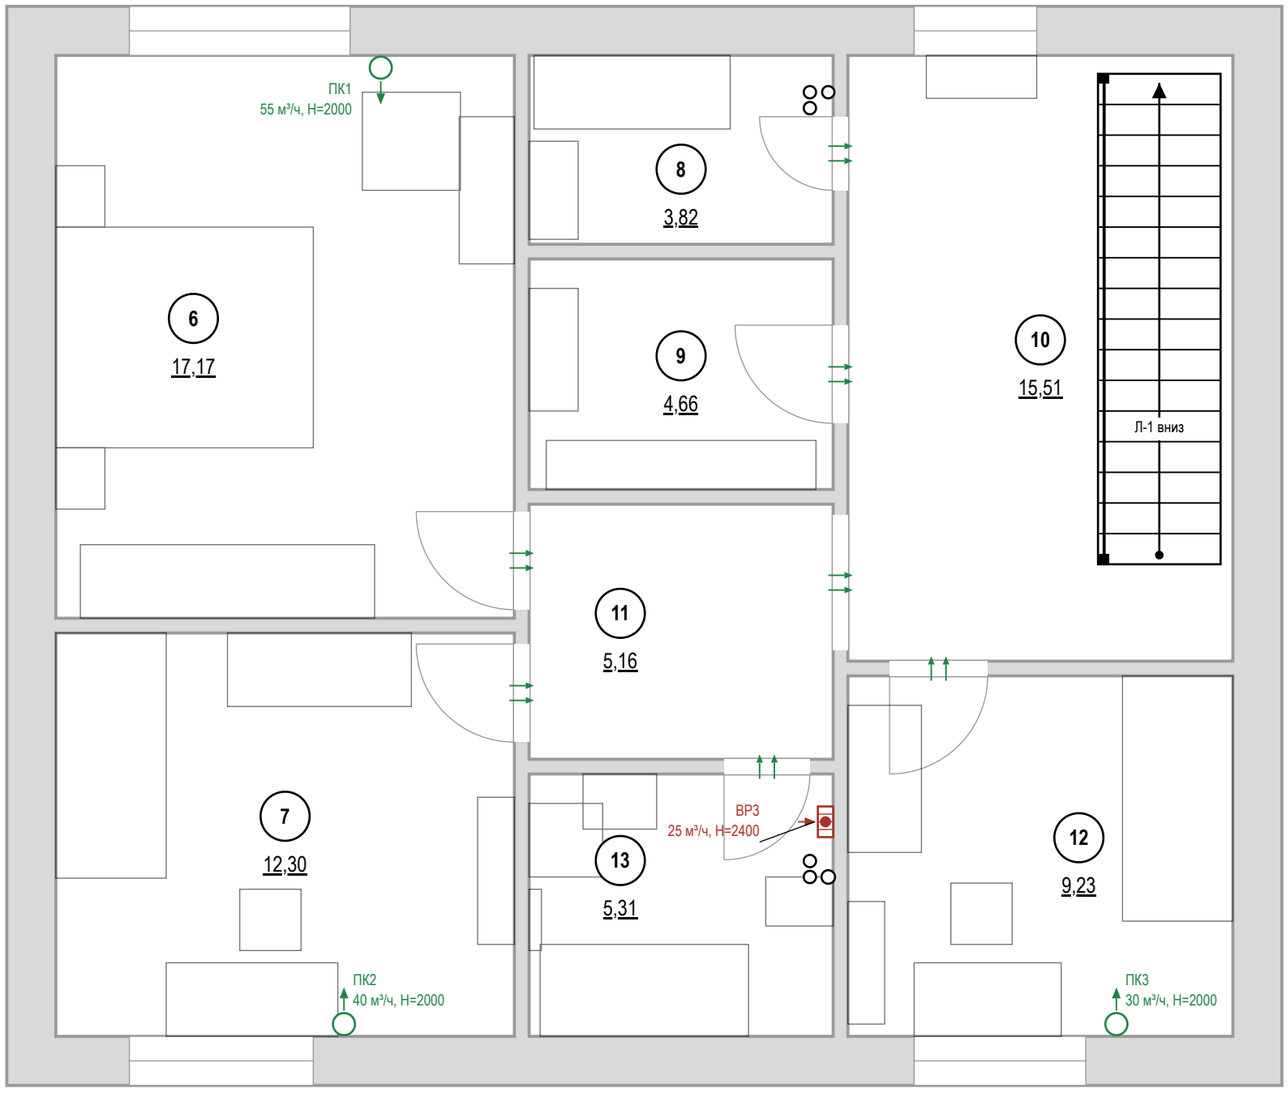


## Условные обозначения

- стояк: К1 — канализация, В1 — ХВС, Т3 — ГВС
- 1 — номер помещения, площадь м²
- вытяжная решётка с бытовым вентилятором и обратным клапаном: марка, расход, Н
- приточный клапан (КИВ) в наружной стене: марка, расход, Н центра
- переток: зазор под полотном или переточная решётка

## Воздухообмен, м³/ч

| № | Помещение | Выт. норма | Выт. проект | Прит. норма | Прит. проект | Устройства |
|---|---|---|---|---|---|---|
| 6 | Спальня родителей | | | 52 | 55 | ПК1 |
| 7 | Детская | | | 37 | 40 | ПК2 |
| 8 | Гардеробная | 2 | | | | переток |
| 9 | Кладовая | 3 | | | | переток |
| 12 | Детская вторая | | | 28 | 30 | ПК3 |
| 13 | Санузел второго этажа | 50 | **25 !** | | | ВР3 |
| | **Итого** | **55** | **25** | **120** | **125** | |

Воздухообмен квартиры — по большей из сумм притока и вытяжки: норма 120 м³/ч, проект 125 м³/ч.
**Приток больше вытяжки на 100 м³/ч — поднять вытяжку.**
**«!» — проект ниже нормы.**

## Примечания

1. Расчёт систем ОВ и подбор оборудования — проектная организация с допуском СРО; лист даёт места, трассы и привязки.
2. Нормы вытяжки — СП 54.13330.2022 (Изм. 1, 2), табл. 7.1: кухня с электроплитой 60 м³/ч, с газовой 100; ванная и совмещённый санузел 50; уборная 25; гардеробная 0,2 ч⁻¹. Приток в жилые — 3 м³/ч на 1 м² (менее 20 м² общей площади на человека), иначе 30 м³/ч на человека.
3. Вентканалы и шахты не сужать, не переносить и не закрывать; вентилятор и кухонная вытяжка — через обратный клапан, без перекрытия естественной тяги.
4. Проектные расходы — не ниже нормы, вытяжка сведена с притоком вентиляторами мокрых помещений. Клапаны — в простенке у окна, центр 2000 мм, не над кроватью, не ближе 300 мм к стоякам отопления; типоразмер — на расход.
5. Переток — зазор под полотнами межкомнатных дверей или переточная решётка.
6. Кондиционирование заданием не предусмотрено; при установке трассы фреона и дренажа (не менее 40 мм/м, в К1 через сифон) и питание заложить до черновых работ.
7. Привязки оборудования — по паспортам приобретённых моделей, до черновых работ.


| | Лист | № док. | Подпись | Дата |
|---|---|---|---|---|
| Дизайнер | Кырлан А.С. | | | 19.10.26 |

Проект: Дом 120 м²

План вентиляции · 2-й этаж

| Стадия | Лист | Листов |
|---|---|---|
| П | 43 | 104 |

выпуск 19.10.2026 № 46d0102a0d · стр. 43 из 104

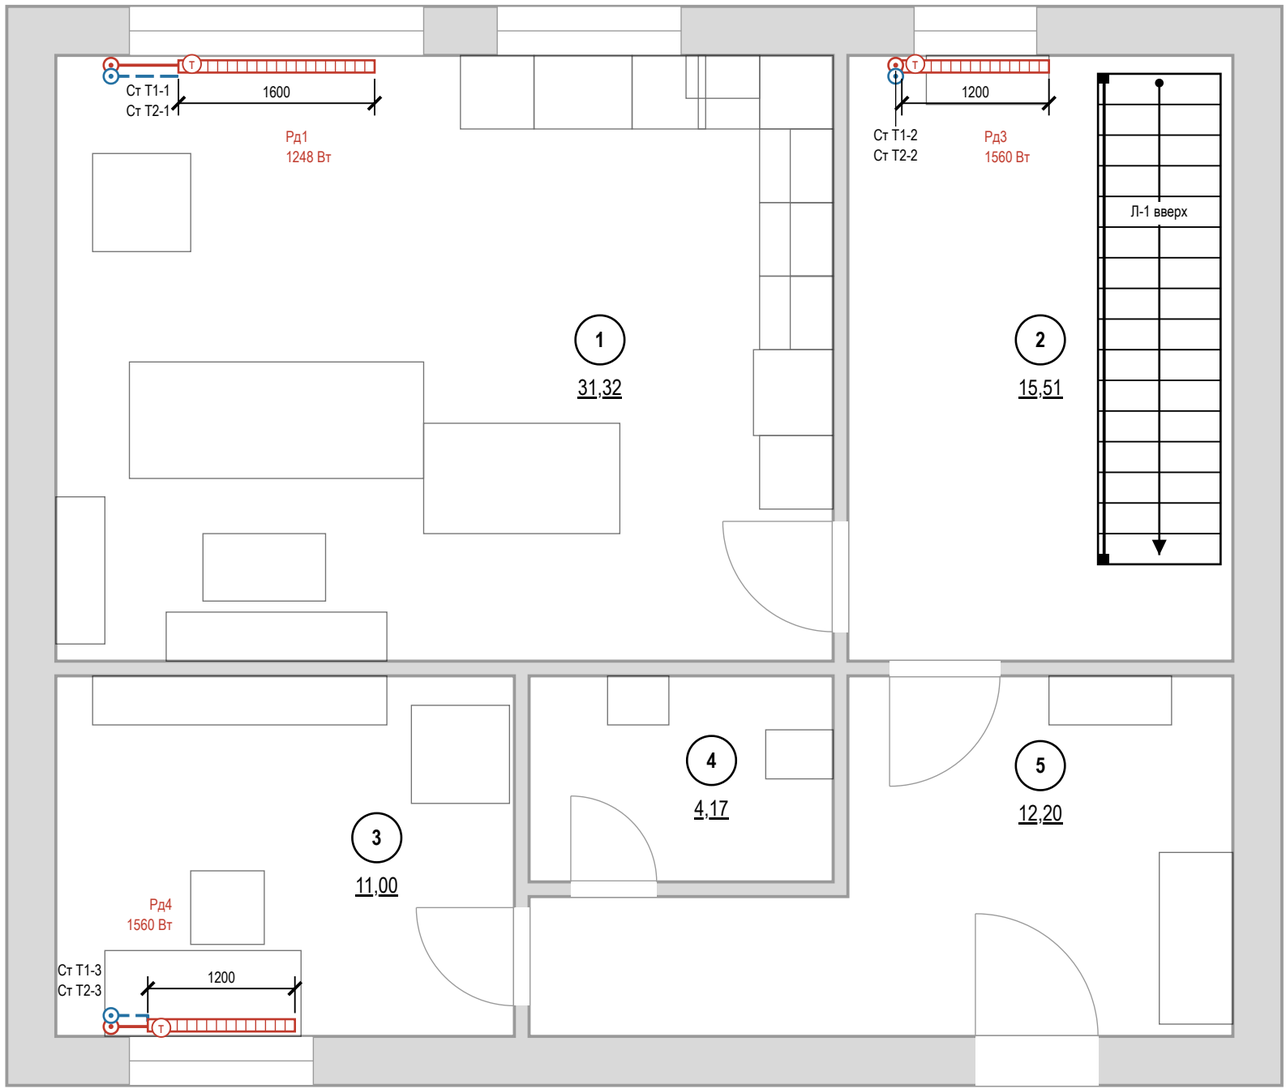


## Условные обозначения

- (1) — номер помещения, площадь м²
- радиатор отопления (марка РО-N, длина по плану)
- (Т) — клапан с термоголовкой на подаче
- стояк отопления, подающий (Ст Т1-N)
- стояк отопления, обратный (Ст Т2-N)
- Т1 — отопление, подающий трубопровод
- Т2 — отопление, обратный трубопровод

## Ведомость радиаторов

| Марка | Помещение | Тип | Д×В×Г, мм | Низ / стена | Q, Вт |
|---|---|---|---|---|---|
| Рд1 | 1. Гостиная-кухня | панельный 22 | 1600×300×100 | 100 / 40 | 1248 |
| Рд3 | 2. Холл с лестницей | панельный 22 | 1200×500×100 | 100 / 40 | 1560 |
| Рд4 | 3. Кабинет | панельный 22 | 1200×500×100 | 100 / 40 | 1560 |

Низ — от чистого пола, стена — зазор до задней панели, мм.


**Привязки — до обмера**
Стояки отопления в исходных данных не заданы: показаны у откосов окон, подводки — принципиально. До черновых работ — обмер стояков и паспорта приборов; лист перевыпустить по факту.

## Примечания

1. Расчёт системы отопления, теплопотерь и подбор приборов — проектная организация с допуском СРО; лист даёт места и привязки.
2. Тип, длина и мощность радиаторов — по теплотехническому расчёту; лист задаёт места, зазоры и подключение.
3. Зазоры радиатора: низ не менее 100 мм от чистого пола, верх не менее 100 мм до подоконника, 30–50 мм от стены до задней панели; центр по оси окна с допуском ±20 мм.
4. Радиаторы не закрывать глухими коробами и мебелью; перенос и замена приборов в многоквартирном доме — переустройство, согласование с управляющей организацией (ЖК РФ ст. 25–26); вынос на лоджию запрещён.
5. Трубы отопления через межквартирные стены не прокладывать (СП 51.13330.2011, п. 9.19); через перекрытия и перегородки — в гильзах.
6. Привязки приборов и подводок — по паспортам приобретённых радиаторов и клапанов, до черновых работ.
7. До закрытия отделкой трубопроводы отопления испытать гидростатическим давлением с оформлением акта (СП 73.13330.2016, 7.2–7.3).

| | | | | | |
|---|---|---|---|---|---|
| | | | | | Проект: Дом 120 м² |
| | Лист | № док. | Подпись | Дата | План отопления · 1-й этаж |
| Дизайнер | Кырлан А.С. | | | 19.10.26 | Стадия: П; Лист: 44; Листов: 104 |

выпуск 19.10.2026 № 46d0102a0d · стр. 44 из 104

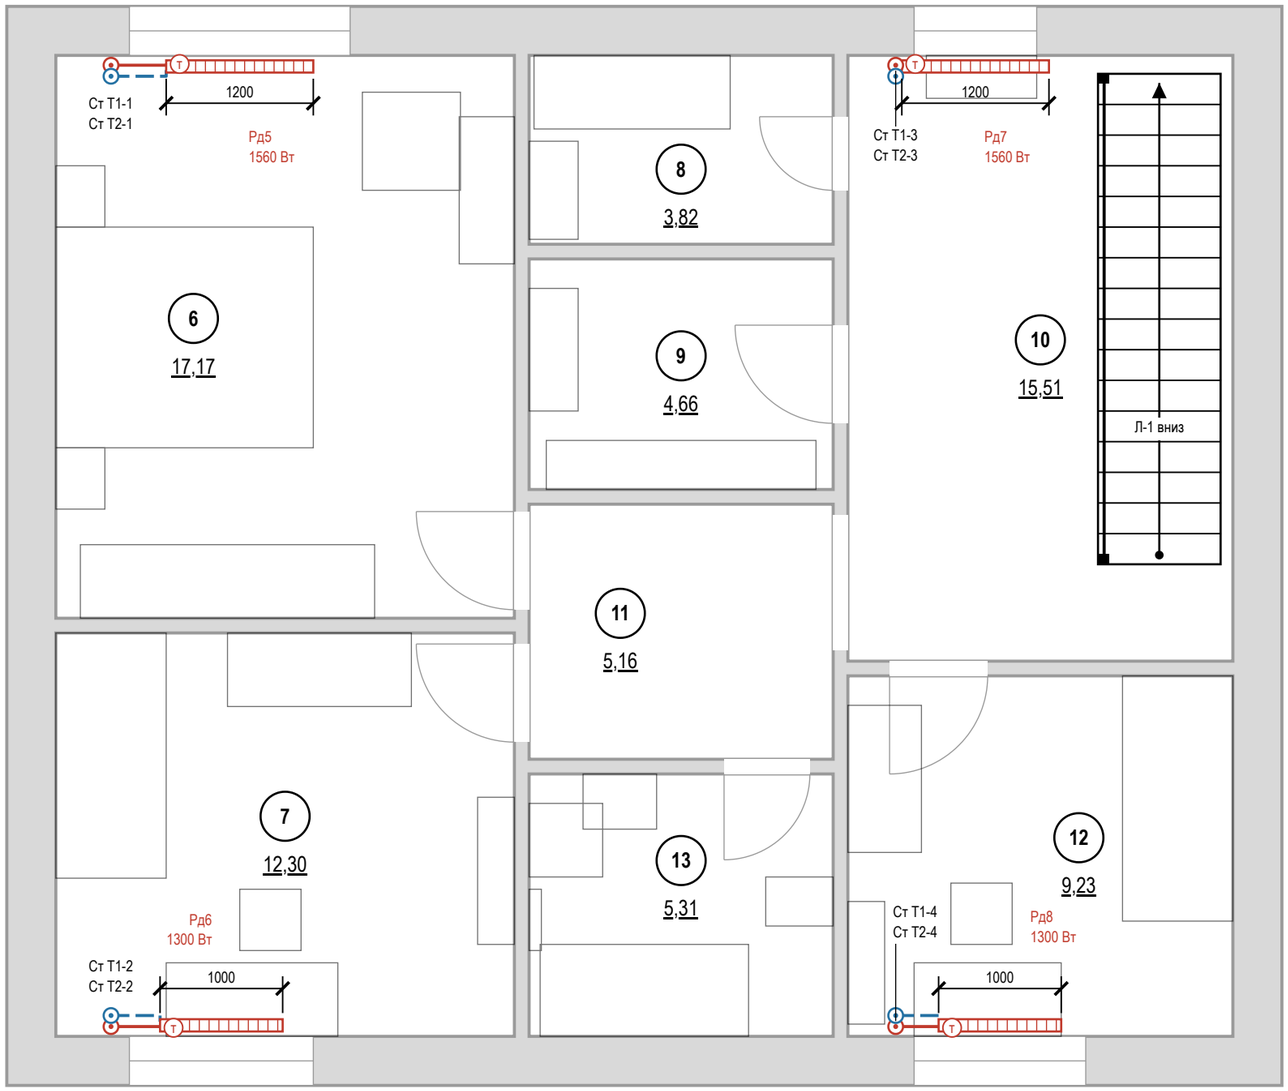


## Условные обозначения

- (1) — номер помещения, площадь м²
- радиатор отопления (марка РО-N, длина по плану)
- (Т) — клапан с термоголовкой на подаче
- стояк отопления, подающий (Ст Т1-N)
- стояк отопления, обратный (Ст Т2-N)
- Т1 — отопление, подающий трубопровод
- Т2 — отопление, обратный трубопровод

## Ведомость радиаторов

| Марка | Помещение | Тип | Д×В×Г, мм | Низ / стена | Q, Вт |
|---|---|---|---|---|---|
| Рд5 | 6. Спальня родителей | панельный 22 | 1200×500×100 | 100 / 40 | 1560 |
| Рд6 | 7. Детская | панельный 22 | 1000×500×100 | 100 / 40 | 1300 |
| Рд7 | 10. Холл второго этажа | панельный 22 | 1200×500×100 | 100 / 40 | 1560 |
| Рд8 | 12. Детская вторая | панельный 22 | 1000×500×100 | 100 / 40 | 1300 |

Низ — от чистого пола, стена — зазор до задней панели, мм.


**Привязки — до обмера**
Стояки отопления в исходных данных не заданы: показаны у откосов окон, подводки — принципиально. До черновых работ — обмер стояков и паспорта приборов; лист перевыпустить по факту.

## Примечания

1. Расчёт системы отопления, теплопотерь и подбор приборов — проектная организация с допуском СРО; лист даёт места и привязки.
2. Тип, длина и мощность радиаторов — по теплотехническому расчёту; лист задаёт места, зазоры и подключение.
3. Зазоры радиатора: низ не менее 100 мм от чистого пола, верх не менее 100 мм до подоконника, 30–50 мм от стены до задней панели; центр по оси окна с допуском ±20 мм.
4. Радиаторы не закрывать глухими коробами и мебелью; перенос и замена приборов в многоквартирном доме — переустройство, согласование с управляющей организацией (ЖК РФ ст. 25–26); вынос на лоджию запрещён.
5. Трубы отопления через межквартирные стены не прокладывать (СП 51.13330.2011, п. 9.19); через перекрытия и перегородки — в гильзах.
6. Привязки приборов и подводок — по паспортам приобретённых радиаторов и клапанов, до черновых работ.
7. До закрытия отделкой трубопроводы отопления испытать гидростатическим давлением с оформлением акта (СП 73.13330.2016, 7.2–7.3).

| | | | | | |
|---|---|---|---|---|---|
| | | | | | Проект: Дом 120 м² |
| | Лист | № док. | Подпись | Дата | |
| Дизайнер | Кырлан А.С. | | | 19.10.26 | План отопления · 2-й этаж |

| Стадия | Лист | Листов |
|---|---|---|
| П | 45 | 104 |

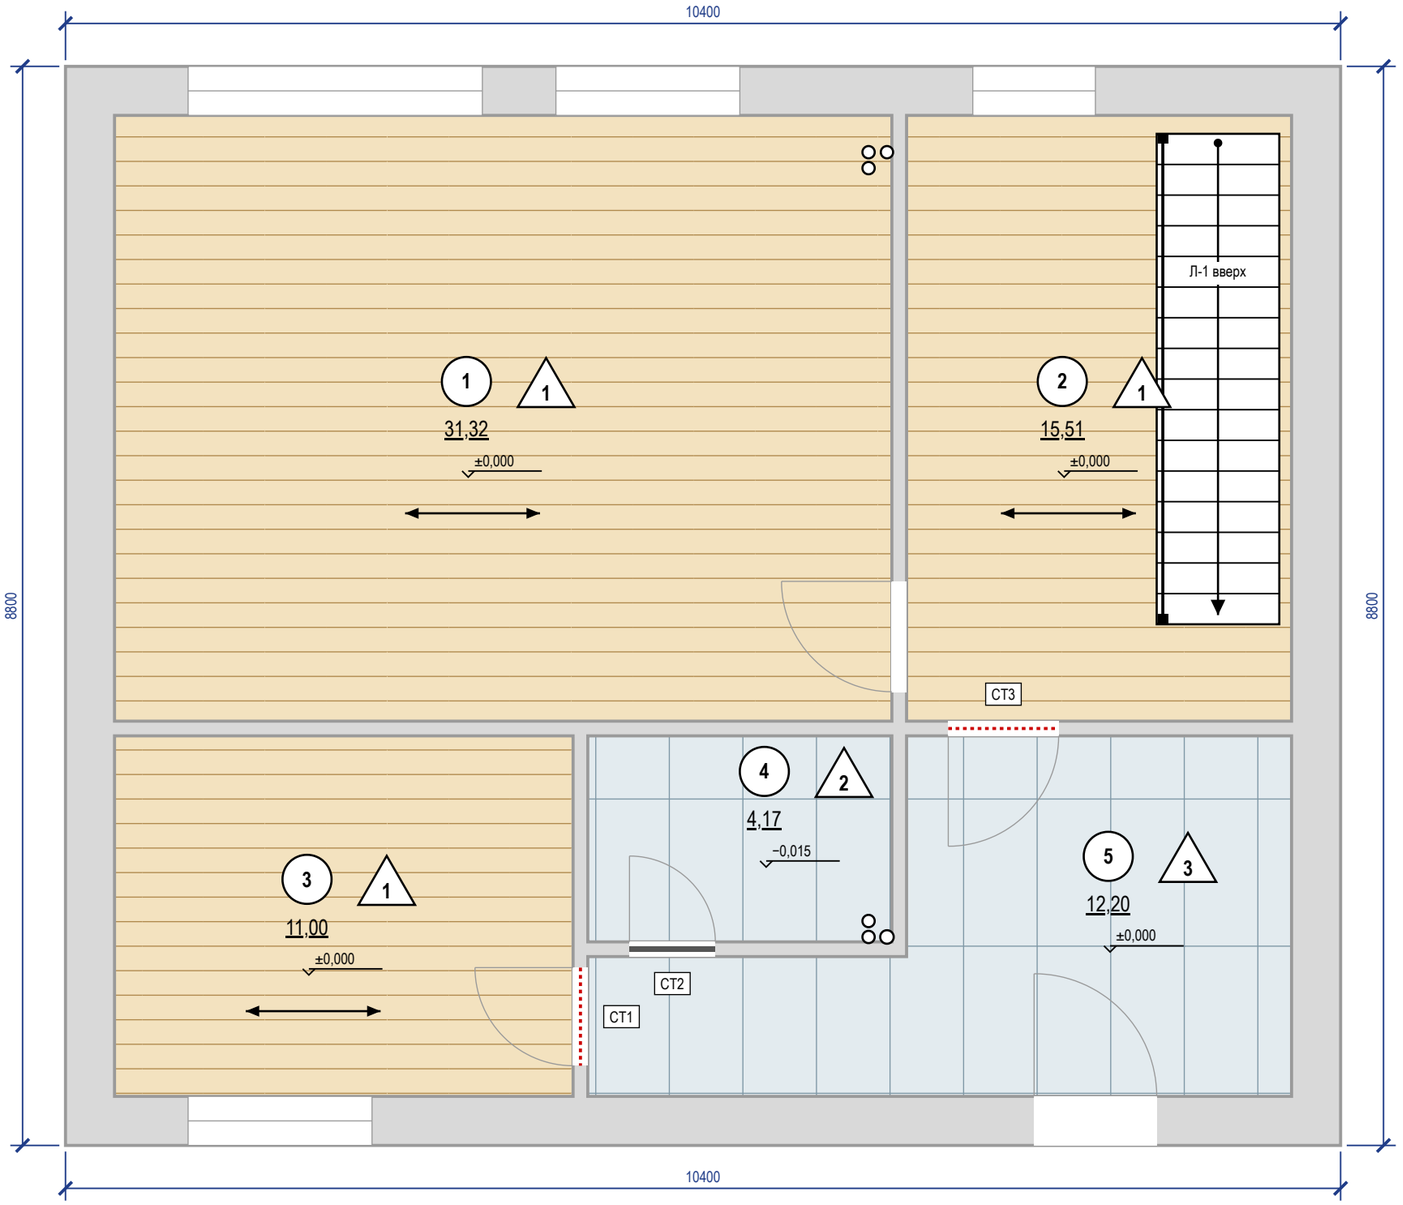


## Экспликация полов

| Номер помещения | Тип пола | Схема пола | Данные элементов пола (наименование, толщина, основание), мм | Площадь, м² |
|---|---|---|---|---|
| 1, 2, 3 | 1 | | Инженерная доска на клею — 14<br>Стяжка ЦПС М200 — 50<br>Плита перекрытия<br>Всего 64 мм; ЧП ±0,000, верх плиты −0,064 | 57,83 |
| 4 | 2 | | Керамогранит на клею С2 TE S1 — 14<br>Гидроизоляция обмазочная, 2 слоя, с заведением на стены 200 мм — 2<br>Стяжка ЦПС М200 — 33<br>Плита перекрытия<br>Всего 49 мм; ЧП −0,015, верх плиты −0,064 | 4,17 |
| 5 | 3 | | Керамогранит на клею С2 TE S1 — 14<br>Стяжка ЦПС М200 — 50<br>Плита перекрытия<br>Всего 64 мм; ЧП ±0,000, верх плиты −0,064 | 12,20 |
| | | | **Итого** | **74,20** |

## Спецификация плинтусов

| Наименование | Помещения | Длина, м (с запасом) |
|---|---|---|
| Плинтус МДФ под покраску 80×16, крепление к стене, окраска в цвет Tikkurila G503 | 1, 2, 3, 5 | 69 |

## Отметки по высоте

**±0,000** чистый пол пом. 1–3, 5; отсчёт высот
**−0,015** чистый пол пом. 4, ниже на 15 мм
**−0,064** верх плиты — расчёт, не замер (задание на обмер)
**сущ. пол** снимается до плиты; не замерен (задание на обмер)

## Примечания

1. За отметку ±0,000 принят чистый пол, не существующий (блок отметок). Площади — по чистым размерам помещений, м²; размеры — в мм.
2. Стык разнотипных покрытий — по оси дверного полотна (под полотном в закрытом положении); решение стыка — по ведомости стыков.
3. Пол санузлов ниже смежных помещений на 15 мм за счёт меньшей толщины стяжки (верх плиты общий — по экспликации полов); гидроизоляция по стяжке с заведением на стены не менее 200 мм (СП 29.13330.2011, п. 7.2), до облицовки — тест проливом и акт скрытых работ.
4. Трубопроводы в конструкции пола не прокладываются: пирог пола 49–64 мм не вмещает выпуски канализации с уклоном — выпуски К1 ведутся по стенам над чистым полом в коробах.
5. Штучные покрытия (инженерная доска): направление — по стрелке; влажность основания по СМ не более 2,0 % (по ТУ изготовителя).
6. Ровность основания — просвет под 2-метровой рейкой не более 2 мм: пом. 1, 2, 3 (инженерная доска), пом. 4, 5 (керамогранит); проверить до укладки покрытия (СП 71.13330.2017, табл. 8.5).
7. Сетка на плитке — условная, в размер формата; точка старта и раскладка — по листу раскладки плитки.
8. Пироги полов — по экспликации полов: слои сверху вниз, толщины в мм; гидроизоляция мокрых зон — в пироге и в ведомости отделки; схема пола — без масштаба.



| | | | | | |
|---|---|---|---|---|---|
| | | | | | Проект: Дом 120 м² |
| | Лист | № док. | Подпись | Дата | План покрытий пола · 1-й этаж |
| Дизайнер | Кырлан А.С. | | | 19.10.26 | |

| Стадия | Лист | Листов |
|---|---|---|
| П | 46 | 104 |

выпуск 19.10.2026 № 46d0102a0d · стр. 46 из 104




## Экспликация полов
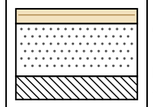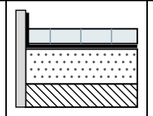
| Номер помещения | Тип пола | Схема пола | Данные элементов пола (наименование, толщина, основание), мм | Площадь, м² |
|---|---|---|---|---|
| 6, 7, 8, 10, 11, 12 | 1 |  | Инженерная доска на клею — 14<br>Стяжка ЦПС М200 — 50<br>Плита перекрытия<br>Всего 64 мм; ЧП ±0,000, верх плиты −0,064 | 63,19 |
| 9 | 2 | | Инженерная доска, 1167-4250, 2100×127 мм, на клею<br>ЧП ±0,000 | 4,66 |
| 13 | 3 |  | Керамогранит на клею С2 TE S1 — 14<br>Гидроизоляция обмазочная, 2 слоя, с заведением на стены 200 мм — 2<br>Стяжка ЦПС М200 — 33<br>Плита перекрытия<br>Всего 49 мм; ЧП −0,015, верх плиты −0,064 | 5,31 |
| | | | **Итого** | **73,16** |

## Спецификация плинтусов

| Наименование | Помещения | Длина, м (с запасом) |
|---|---|---|
| Плинтус МДФ под покраску 80×16, крепление к стене, окраска в цвет Tikkurila G503 | 6, 8, 10, 11 | 47 |
| SX165, h = 69 мм, крепление к стене, окраска в цвет Tikkurila G503 | 7, 9, 12 | 36 |

## Отметки по высоте

**±0,000** чистый пол пом. 6–12; отсчёт высот
**−0,015** чистый пол пом. 13, ниже на 15 мм
**−0,064** верх плиты — расчёт, не замер (задание на обмер)
**сущ. пол** снимается до плиты; не замерен (задание на обмер)


## Примечания

1. За отметку ±0,000 принят чистый пол, не существующий (блок отметок). Площади — по чистым размерам помещений, м²; размеры — в мм.
2. Стык разнотипных покрытий — по оси дверного полотна (под полотном в закрытом положении); решение стыка — по ведомости стыков.
3. Пол санузлов ниже смежных помещений на 15 мм за счёт меньшей толщины стяжки (верх плиты общий — по экспликации полов); гидроизоляция по стяжке с заведением на стены не менее 200 мм (СП 29.13330.2011, п. 7.2), до облицовки — тест проливом и акт скрытых работ.
4. Трубопроводы в конструкции пола не прокладываются: пирог пола 49–64 мм не вмещает выпуски канализации с уклоном — выпуски К1 ведутся по стенам над чистым полом в коробах.
5. Штучные покрытия (инженерная доска): направление — по стрелке; влажность основания по СМ не более 2,0 % (по ТУ изготовителя).
6. Ровность основания — просвет под 2-метровой рейкой не более 2 мм: пом. 6, 7, 8, 9, 10, 11, 12 (инженерная доска), пом. 13 (керамогранит); проверить до укладки покрытия (СП 71.13330.2017, табл. 8.5).
7. Сетка на плитке — условная, в размер формата; точка старта и раскладка — по листу раскладки плитки.
8. Пироги полов — по экспликации полов: слои сверху вниз, толщины в мм; гидроизоляция мокрых зон — в пироге и в ведомости отделки; схема пола — без масштаба.


| | | | | | |
|---|---|---|---|---|---|
| | | | | | Проект: Дом 120 м² |
| | Лист | № док. | Подпись | Дата | План покрытий пола · 2-й этаж |
| Дизайнер | Кырлан А.С. | | | 19.10.26 | |

| Стадия | Лист | Листов |
|---|---|---|
| П | 47 | 104 |

**Фрагмент 1. Санузел гостевой (пом. 4). Пол 600×600, шов 2 мм, М 1:25**

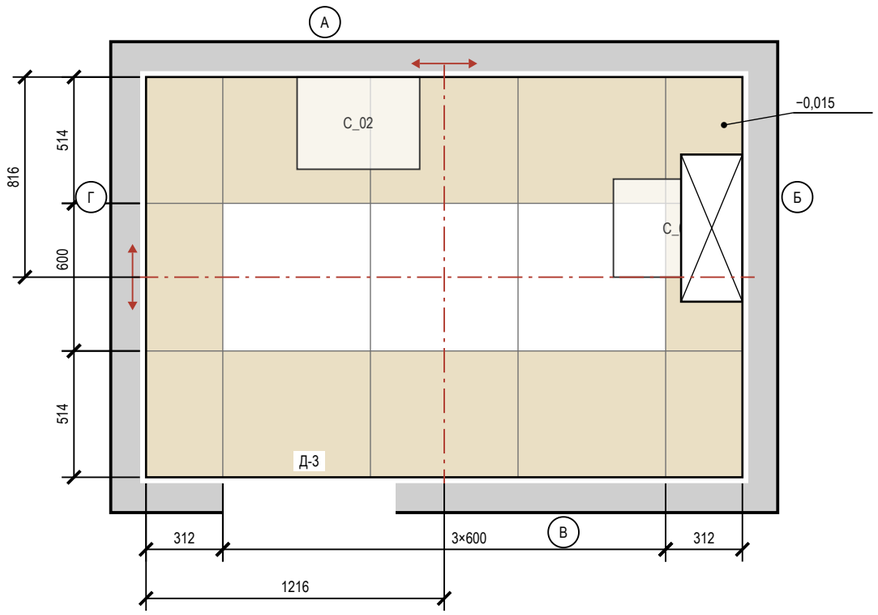


**Фрагмент 2. Санузел второго этажа (пом. 13). Пол 600×600, шов 2 мм, М 1:25**

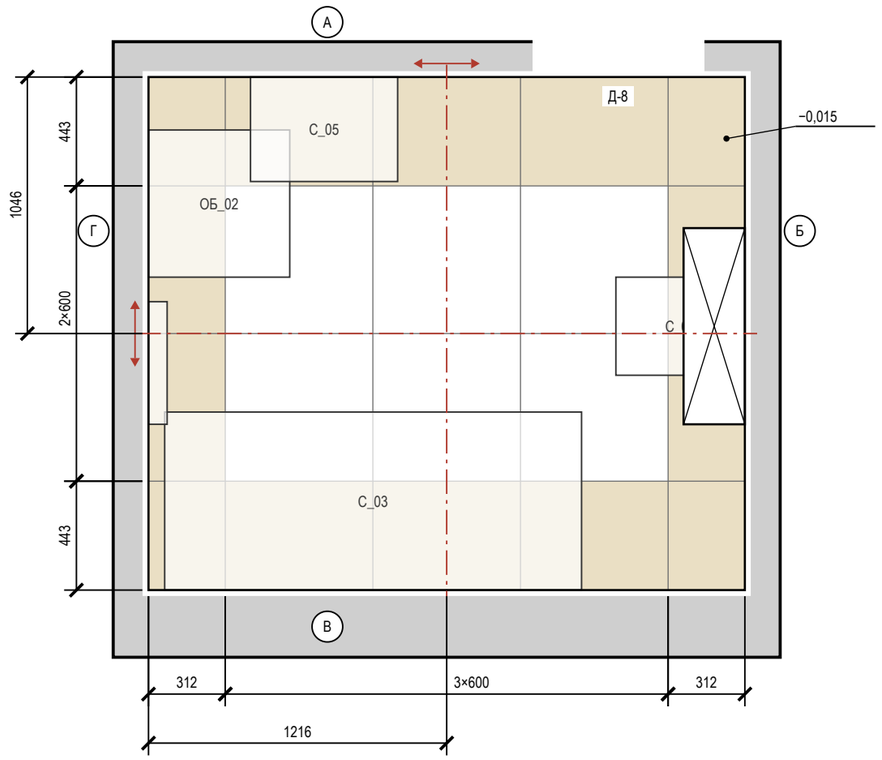


## Примечания

1. Раскладка от чистовых размеров: стены санузлов теряют 10 + 5 + 9 = 24 мм на сторону (штукатурка, клей, плитка); подрезки чистые, без шва.
2. Старт — от центра помещения (штрихпунктир, стрелки направление укладки); размер старта — от чистовых стен Г и А.
3. Раскладка пола «Прихожая» и фартука «Гостиная-кухня» и фартука «Гостиная-кухня» — на листе «Раскладка плитки. Прихожая. Фартук кухни».
4. Калибр партии не задан — до укладки замерить (рабочий размер W, ГОСТ 13996-2019) и пересчитать подрезки.
5. Количество: целые по раскладке + по одной на подрезку, запас 10 %; один артикул — одна партия и тон. Исключены поддон, короб, проёмы и места за коробом; S — по чистым граням: стены нетто = зона облицовки по ведомости отделки − место за коробом инсталляции 1,68 м² (плитку за коробом не кладут), короб отдельной строкой.
6. Клей C2 TE S1 Ceresit CM 17; C2 TE S1 (ГОСТ Р 56387-2018), затирка CG2WA Mapei Ultracolor Plus 132; CG2WA; расход — по ТУ выбранной марки.
7. Гидроизоляция: пол и стены 200 мм от ЧП; над ванной — до 2000 и 300 мм за борт (см. развёртки); акт скрытых работ, пролив 24 ч.
8. Швы пола совмещены со швами стены А; по периметру — демпферная лента.
9. Отметка чистого пола −0,015, порог 15 мм; стык с соседним покрытием — по оси полотна двери.

## Ведомость плитки

| Помещение, поверхность | Плитка, код | Формат | Шов | S, м² | Целых | Подр. | С запасом |
|---|---|---|---|---|---|---|---|
| Санузел гостевой, пол | аналог: керамогранит под травертин | 600×600 | 2 | 4,17 | 3 | 12 | 17 |
| Санузел гостевой, стены А–Г | аналог: керамогранит под травертин | 600×1200 | 2 | 16,68 | 11 | 21 | 36 |
| Санузел гостевой, короб инсталляции | аналог: керамогранит под травертин | 600×1200 | 2 | 1,47 | 1 | 3 | 5 |
| Санузел второго этажа, пол | аналог: керамогранит под травертин | 600×600 | 2 | 5,31 | 6 | 14 | 22 |
| Санузел второго этажа, стены А–Г | аналог: керамогранит под травертин | 600×1200 | 2 | 18,10 | 16 | 20 | 40 |
| Санузел второго этажа, короб инсталляции | аналог: керамогранит под травертин | 600×1200 | 2 | 1,76 | 0 | 6 | 7 |
| Прихожая, пол | A8UZ | 600×1200 | 2 | 12,20 | 4 | 14 | 20 |
| Гостиная-кухня, фартук (ст. А) | аналог: керамогранит под травертин, матовый | 1200×600 | 2 | 0,65 | 0 | 3 | 4 |
| Гостиная-кухня, фартук (ст. Б) | аналог: керамогранит под травертин, матовый | 1200×600 | 2 | 1,35 | 0 | 2 | 3 |
| Итого 600×600 | | | | 9,48 | 9 | 26 | 39 |
| **Итого 600×1200** | | | | **52,21** | **32** | **69** | **115** |

## Ведомость материалов

| Материал | Класс, код | Норма расхода | Кол-во |
|---|---|---|---|
| Затирка | CG2WA Mapei Ultracolor Plus 132 | (a+b)/ab·шов·t·1,6 | 4,1 кг |
| Затирка | CG2WA | (a+b)/ab·шов·t·1,6 | 0,9 кг |
| Клей | C2 TE S1 Ceresit CM 17 | 1,5 кг/м²·мм, слой 5 | 402 кг (17 меш.) |
| Клей | C2 TE S1 | 1,5 кг/м²·мм, слой 5 | 92 кг (4 меш.) |
| Гидроизоляция | обмазочная, 2 слоя: пол, стены по периметру и зоны замачивания | по ТУ | 19,6 м² |
| Демпф. лента | по периметру пола из плитки | | 27,6 м |

## Условные обозначения


- плитка целая; тонкая линия — шов
- плитка с подрезкой (размер — на цепочке)
- ось старта; стрелки — направление укладки
- сантехприбор: габарит, высота по практике
- короб инсталляции: плитка пола — до короба
- отметка чистого пола на полке выноски, м
- (А) обозначение стены А–Г (как на развёртках)

| | | | | | |
|---|---|---|---|---|---|
| | | | | | Проект: Дом 120 м² |
| | Лист | № док. | Подпись | Дата | Раскладка плитки. Планы полов |
| Дизайнер | Кырлан А.С. | | | 19.10.26 | |


| Стадия | Лист | Листов |
|---|---|---|
| П | 48 | 104 |

выпуск 19.10.2026 № 46d0102a0d · стр. 48 из 104


**Фрагмент 1. Прихожая (пом. 5). Пол 600×1200, шов 2 мм, М 1:25**

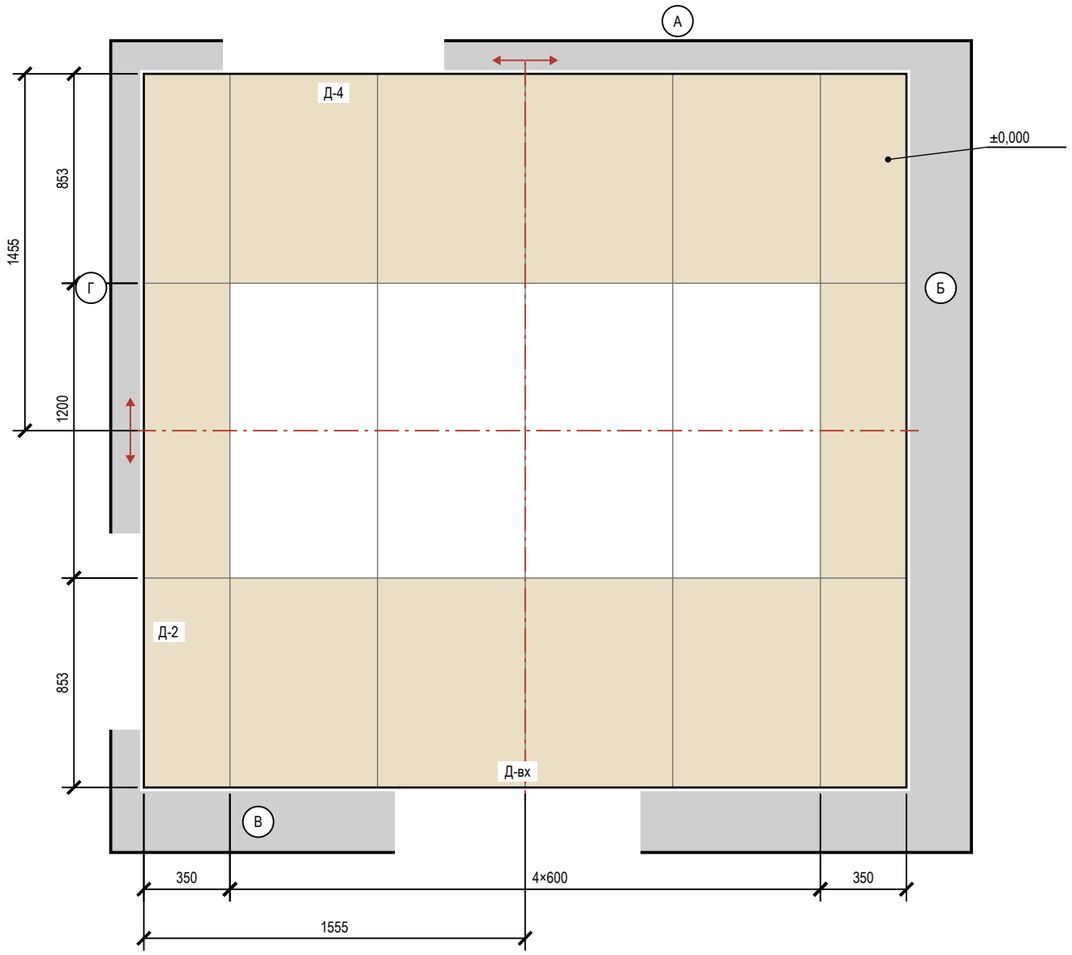


**Фрагмент 2. Гостиная-кухня (пом. 1), фартук, стена А. 1200×600, шов 2 мм, М 1:25**

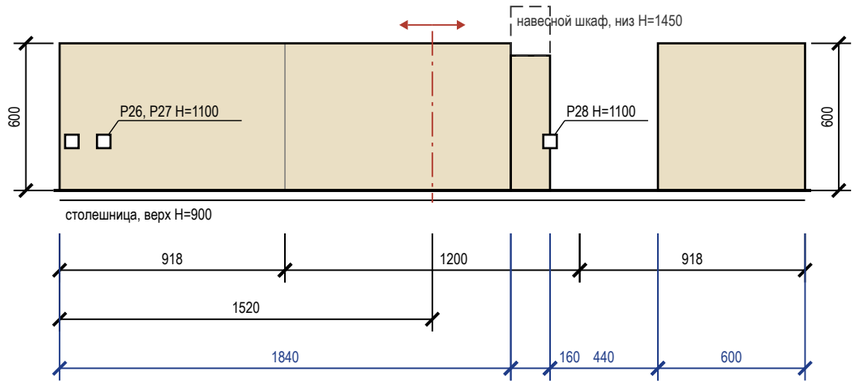


**Фрагмент 3. Гостиная-кухня (пом. 1), фартук, стена Б. 1200×600, шов 2 мм, М 1:25**

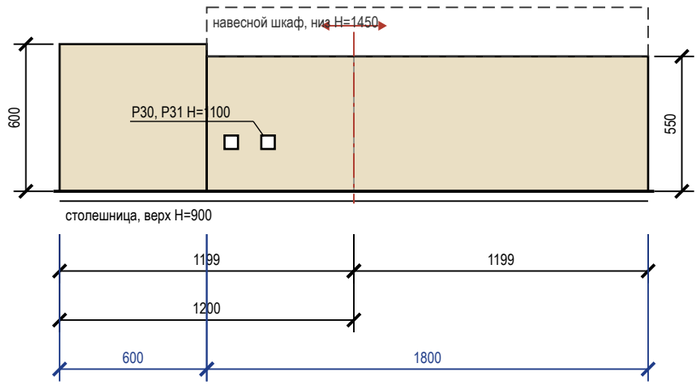


## Условные обозначения

- плитка целая; тонкая линия — шов
- плитка с подрезкой (размер — на цепочке)
- ось старта; стрелки — направление укладки
- электроточка: марка и Н — по листам ЭОМ
- столешница (верх)
- навесной шкаф над фартуком
- отметка чистого пола на полке выноски, м
- (А) обозначение стены А–Г (как на развёртках)

## Примечания

1. Прихожая: керамогранит 600×1200, длинная сторона — вдоль стен Б и Г, шов 2 мм, прямая раскладка от центра. Стены окрашены: раскладка от чистового контура минус штукатурка и шпаклёвка 15 мм на сторону (принято); подрезки 350 / 853 мм, срез — под плинтус.
2. Прихожая: деформационный зазор по периметру 8–10 мм под плинтусом; в проёмах — стык с соседним покрытием по оси полотна двери. Клей С2 TE S1, затирка CG2WA.
3. Фартук, Гостиная-кухня: 1200×600 горизонтально, шов 2 мм; зоны 1840 мм — 900…1500, 160 мм — 900…1450, 600 мм — 900…1500 (от столешницы до низа навесного шкафа, без шкафа — 600 мм). Старт от центра участка, подрезки 918 мм. Площадь 0,65 м² — как в ведомости отделки.
4. Фартук — после монтажа столешницы, низ на 2–3 мм выше неё, шов со столешницей — санитарный герметик; навесные шкафы — после фартука. Торцы у пенала и стены — профиль или запил 45°.
5. Фартук, Гостиная-кухня: 1200×600 горизонтально, шов 2 мм; зоны 600 мм — 900…1500, 1800 мм — 900…1450 (от столешницы до низа навесного шкафа, без шкафа — 600 мм). Старт от центра участка, подрезки нет мм. Площадь 1,35 м² — как в ведомости отделки.
6. Фартук — после монтажа столешницы, низ на 2–3 мм выше неё, шов со столешницей — санитарный герметик; навесные шкафы — после фартука. Торцы у пенала и стены — профиль или запил 45°.
7. Розетки из таблицы переносятся до черновой электрики: по высоте — на ось ряда плитки, от вертикального шва крупной плитки — не ближе 60 мм. Привязка — от левого края фартука на развёртке.
8. Клей, затирка и итог по форматам — в ведомостях листа «Раскладка плитки. Планы полов».

## Подсчёт плитки

| Поверхность | Формат | S, м² | Целых | Подр. | С запасом |
|---|---|---|---|---|---|
| Прихожая, пол | 600×1200 | 12,20 | 4 | 14 | 20 |
| Гостиная-кухня, фартук (ст. А) | 1200×600 | 0,65 | 0 | 3 | 4 |
| Гостиная-кухня, фартук (ст. Б) | 1200×600 | 1,35 | 0 | 2 | 3 |

## Сдвиг розеток фартука под раскладку


| Точка (ЭОМ) | Проект: от угла / Н | Под раскладку: от угла / Н | Сдвиг, мм |
|---|---|---|---|
| Р26, Р27 | 50, 180 / 1100 | 50, 180 / 1200 | Н +100 — ось ряда |
| Р28 | 2000 / 1100 | 2000 / 1175 | Н +75 — ось ряда |
| Р30, Р31 | 700, 850 / 1100 | 700, 850 / 1175 | Н +75 — ось ряда |

| | | | | | |
|---|---|---|---|---|---|
| | | | | | Проект: Дом 120 м² |
| | Лист | № док. | Подпись | Дата | |
| Дизайнер | Кырлан А.С. | | | 19.10.26 | Раскладка плитки. Прихожая. Фартук кухни |


| Стадия | Лист | Листов |
|---|---|---|
| П | 49 | 104 |

выпуск 19.10.2026 № 46d0102a0d · стр. 49 из 104

## Развёртка стены А

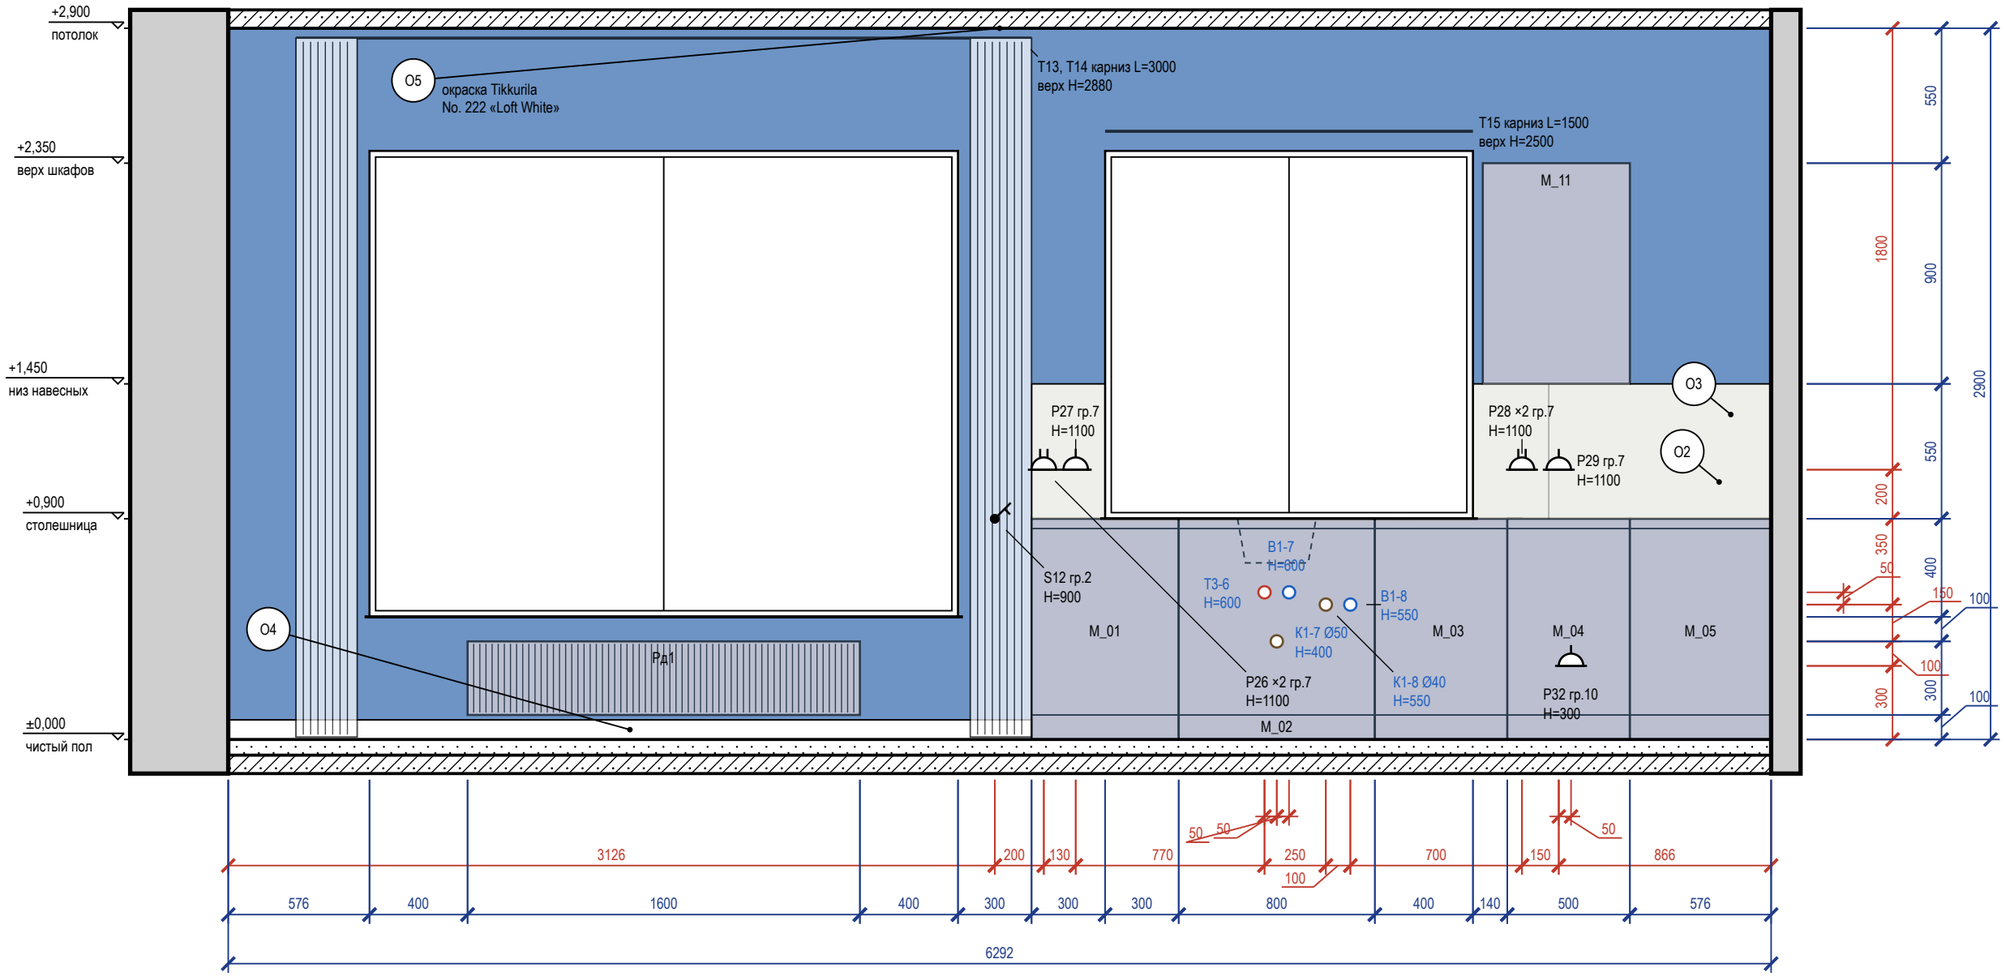


### Схема развёрток (М 1:100)

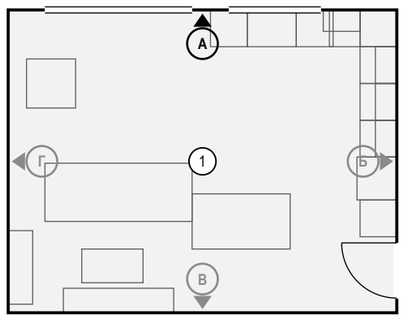


### Ведомость отделки (на листе)

| Марка | Поверхность | Материал, изделие | Цвет, код | Кол. |
|---|---|---|---|---|
| О2 | фартук | керамогранит, 1200×600×9 мм, аналог: керамогранит под травертин, матовый, затирка CG2WA | | 0,8 м² |
| О3 | акцентная стена | окраска, Farrow & Ball Modern Emulsion, матовая, подготовка Q3 | NCS S 3050-R80B «Эгейский синий» | 9,8 м² |
| О4 | плинтус | плинтус МДФ, h 80 мм, аналог: плинтус МДФ под покраску 80×16 | Tikkurila G503 «Calla» | 3,3 м |
| О5 | потолок | окраска, Tikkurila Anti-Reflex 2, глубокоматовая, подготовка Q3 | Little Greene No. 222 «Loft White» | 31,3 м² |

### Примечания


1. Размеры — в мм от чистовых поверхностей стен; условные обозначения и общие указания — лист 2.
2. Выводы ВК — коды и высоты по листу выводов сантехники.
3. Карнизы (шины) — по ведомости текстиля декоратора; длина L и верх H — по развёртке, крепление — до окраски потолка.
4. Выводы кухонной техники — по утверждённому проекту кухни: привязки выводов даются от осей модулей гарнитура.

| | | | | | |
|---|---|---|---|---|---|
| | | | | | Проект: Дом 120 м² |
| | Лист | № док. | Подпись | Дата | Развёртка стены А. Гостиная-кухня (пом. 1), кухонный фронт |
| Дизайнер | Кырлан А.С. | | | 19.10.26 | |


| Стадия | Лист | Листов |
|---|---|---|
| П | 50 | 104 |

выпуск 19.10.2026 № 46d0102a0d · стр. 50 из 104

## Развёртка стены Б

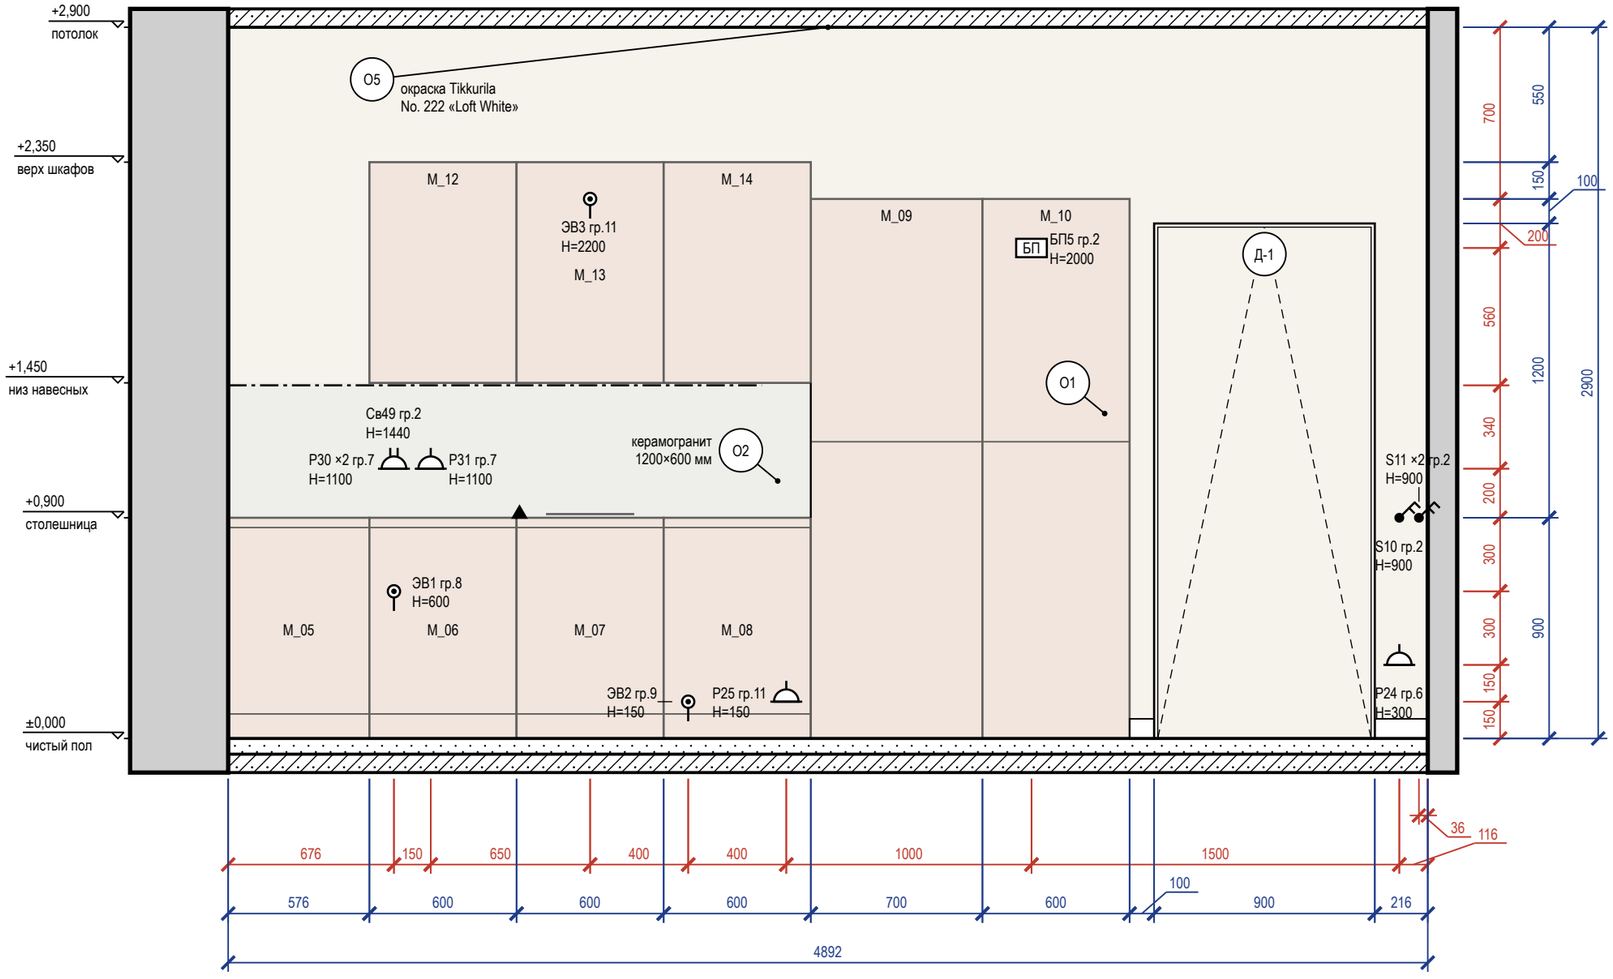


## Схема развёрток (М 1:100)

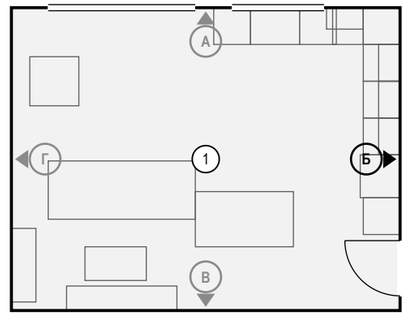


## Ведомость отделки (на листе)

| Марка | Поверхность | Материал, изделие | Цвет, код | Кол. |
|---|---|---|---|---|
| О1 | стены | окраска, Farrow & Ball Modern Emulsion, матовая, подготовка Q3 | Tikkurila G503 «Calla» | 11 м² |
| О2 | фартук | керамогранит, 1200×600×9 мм, аналог: керамогранит под травертин, матовый, затирка CG2WA | | 1,3 м² |
| О4 | плинтус | плинтус МДФ, h 80 мм, аналог: плинтус МДФ под покраску 80×16 | Tikkurila G503 «Calla» | 0,3 м |
| О5 | потолок | окраска, Tikkurila Anti-Reflex 2, глубокоматовая, подготовка Q3 | Little Greene No. 222 «Loft White» | 31,3 м² |


### Примечания

1. Размеры — в мм от чистовых поверхностей стен; условные обозначения и общие указания — лист 2.
2. Двери скрытого монтажа — полотно в плоскости стены, отделка стены по полотну, плинтус прерывается у короба (узел — на листе узлов).
3. Выводы кухонной техники — по утверждённому проекту кухни: привязки выводов даются от осей модулей гарнитура.


| | | | | | |
|---|---|---|---|---|---|
| | | | | | Проект: Дом 120 м² |
| | Лист | № док. | Подпись | Дата | Развёртка стены Б. Гостиная-кухня (пом. 1), кухонный фронт |
| Дизайнер | Кырлан А.С. | | | 19.10.26 | |

| Стадия | Лист | Листов |
|---|---|---|
| П | 51 | 104 |

## Развёртка стены В

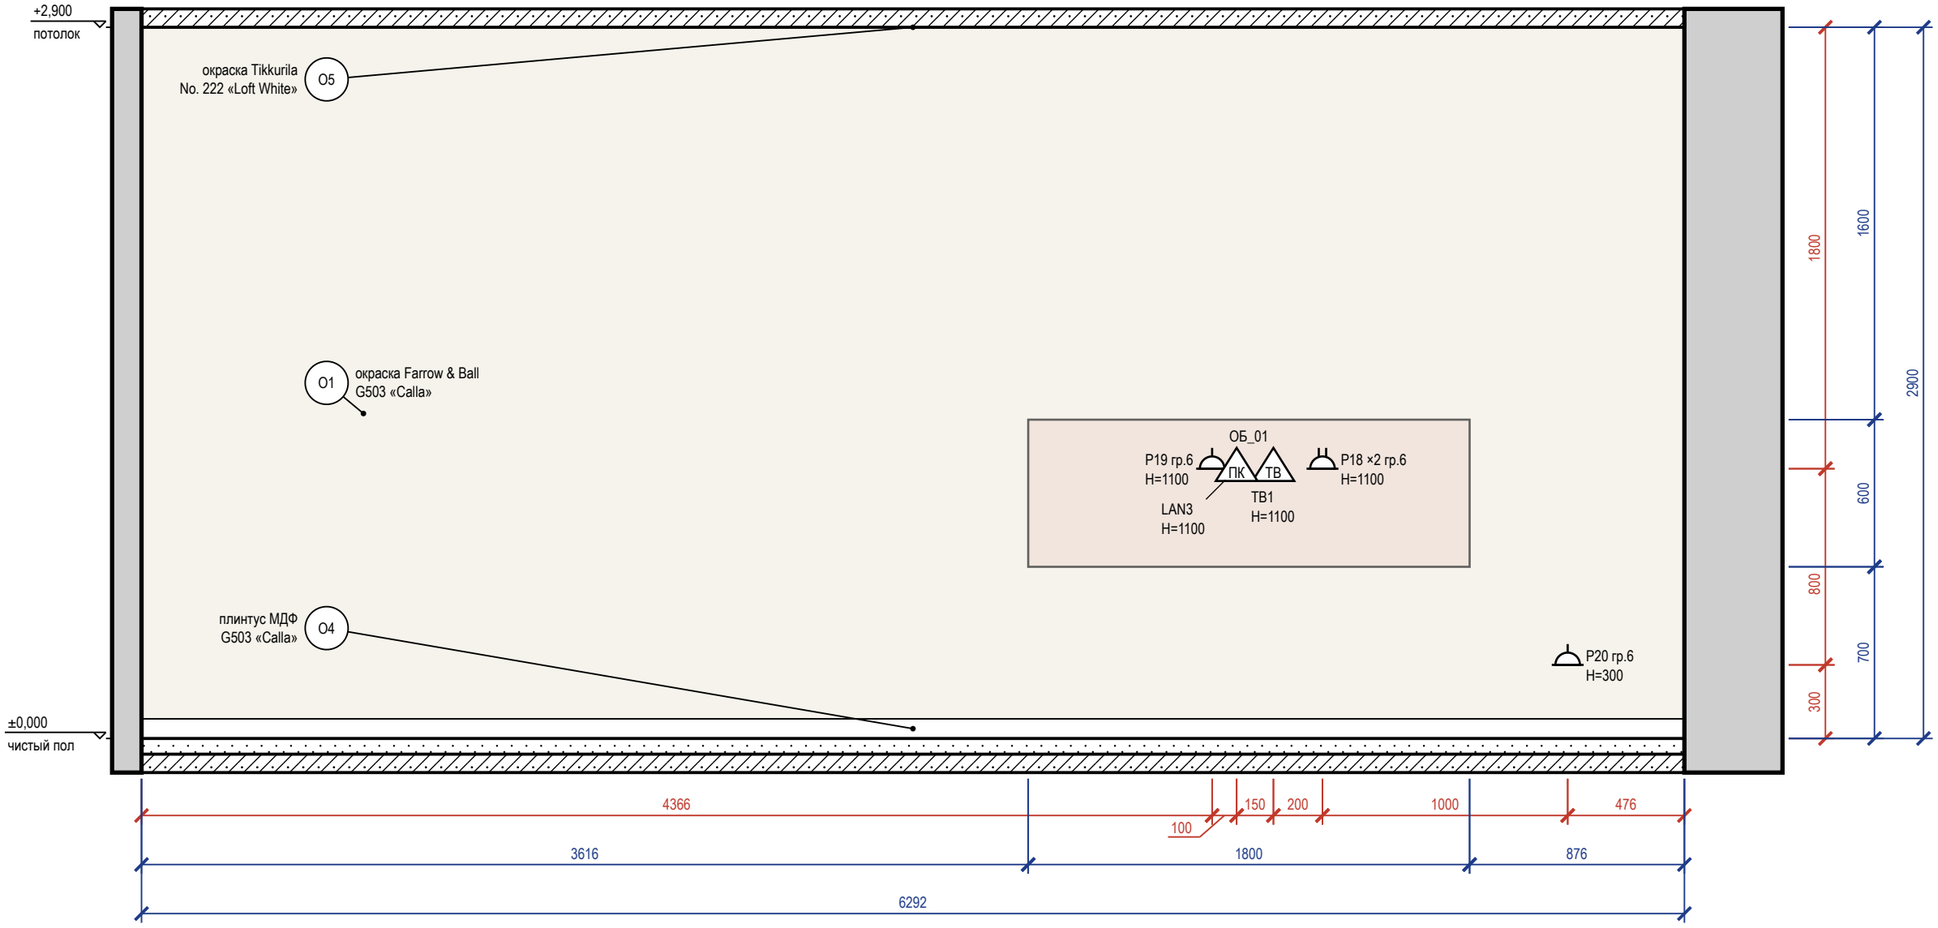


### Схема развёрток (М 1:100)

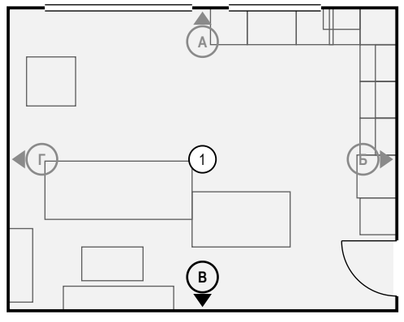


### Ведомость отделки (на листе)

| Марка | Поверхность | Материал, изделие | Цвет, код | Кол. |
|---|---|---|---|---|
| О1 | стены | окраска, Farrow & Ball Modern Emulsion, матовая, подготовка Q3 | Tikkurila G503 «Calla» | 18,2 м² |
| О4 | плинтус | плинтус МДФ, h 80 мм, аналог: плинтус МДФ под покраску 80×16 | Tikkurila G503 «Calla» | 6,3 м |
| О5 | потолок | окраска, Tikkurila Anti-Reflex 2, глубокоматовая, подготовка Q3 | Little Greene No. 222 «Loft White» | 31,3 м² |

### Примечания


1. Размеры — в мм от чистовых поверхностей стен; условные обозначения и общие указания — лист 2.
2. Схема мебели, приборов и декора не является технической документацией для производства мебели; габариты — по паспортам изделий.

| | | | | | |
|---|---|---|---|---|---|
| | | | | | Проект: Дом 120 м² |
| | Лист | № док. | Подпись | Дата | Развёртка стены В. Гостиная-кухня (пом. 1) |
| Дизайнер | Кырлан А.С. | | | 19.10.26 | |


| Стадия | Лист | Листов |
|---|---|---|
| П | 52 | 104 |

выпуск 19.10.2026 № 46d0102a0d · стр. 52 из 104

## Развёртка стены Г

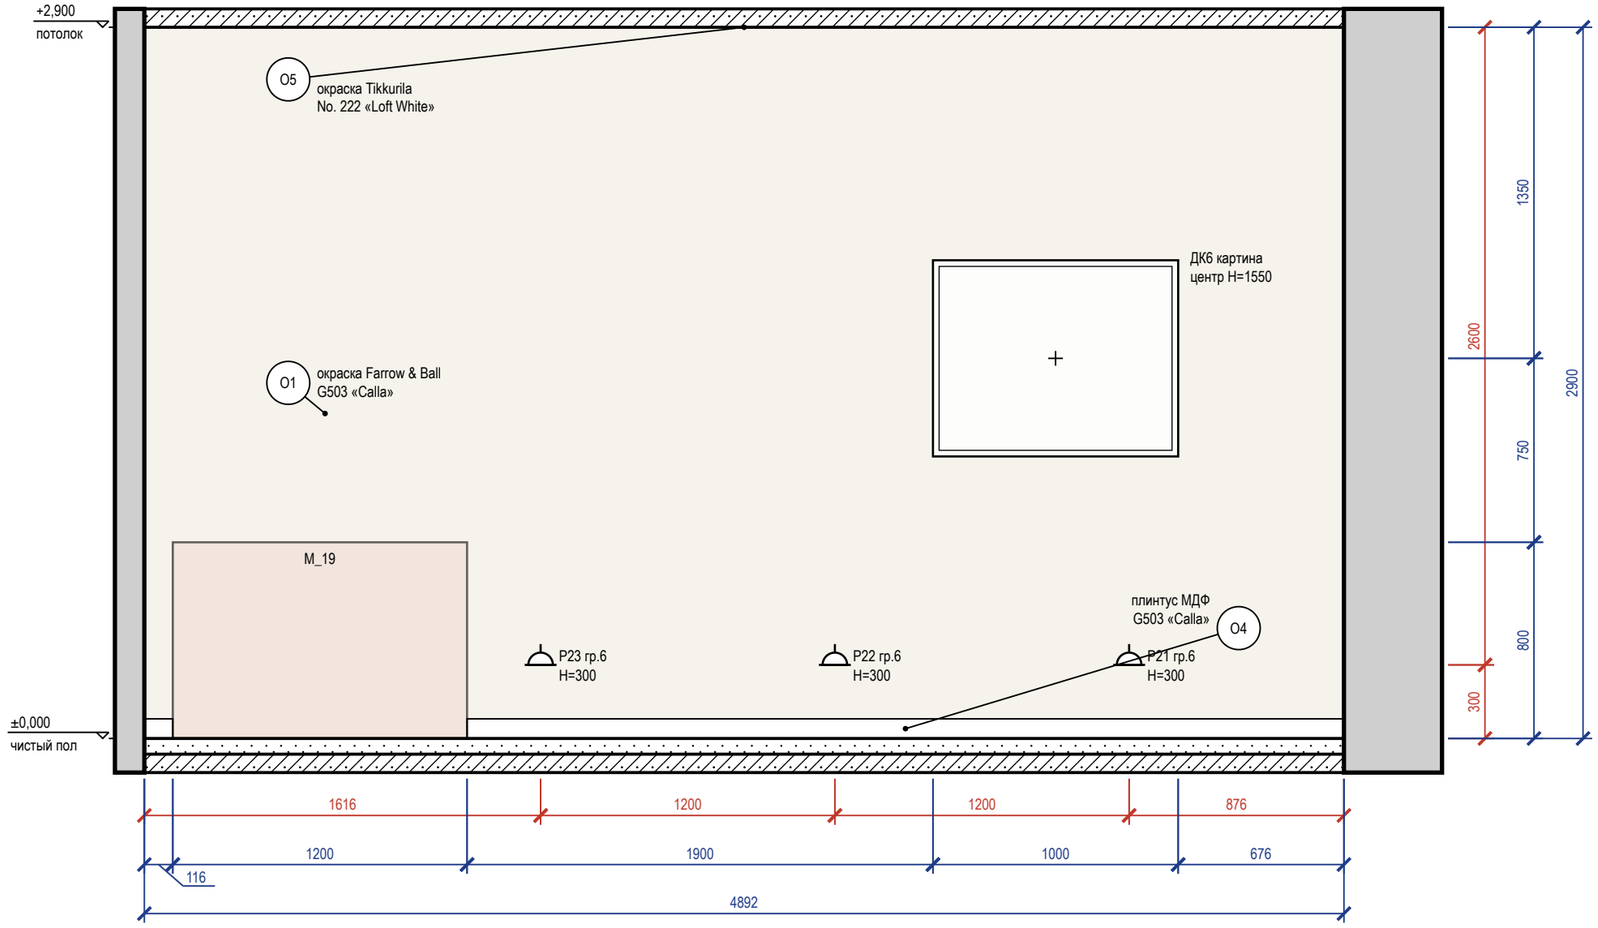


## Схема развёрток (М 1:100)

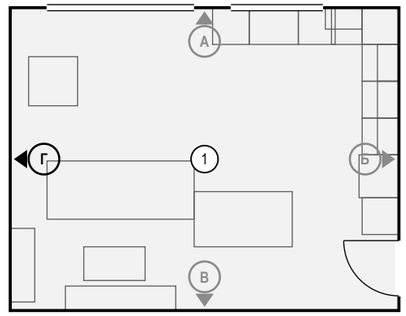


## Ведомость отделки (на листе)

| Марка | Поверхность | Материал, изделие | Цвет, код | Кол. |
|---|---|---|---|---|
| О1 | стены | окраска, Farrow & Ball Modern Emulsion, матовая, подготовка Q3 | Tikkurila G503 «Calla» | 14,2 м² |
| О4 | плинтус | плинтус МДФ, h 80 мм, аналог: плинтус МДФ под покраску 80×16 | Tikkurila G503 «Calla» | 3,7 м |
| О5 | потолок | окраска, Tikkurila Anti-Reflex 2, глубокоматовая, подготовка Q3 | Little Greene No. 222 «Loft White» | 31,3 м² |

## Примечания


1. Размеры — в мм от чистовых поверхностей стен; условные обозначения и общие указания — лист 2.
2. Картины и зеркала крепить к основанию по паспорту изделия (закладные и анкеры — в перечне скрытых работ); крест — ось центра предмета.

| | | | | | |
|---|---|---|---|---|---|
| | | | | | Проект: Дом 120 м² |
| | Лист | № док. | Подпись | Дата | Развёртка стены Г. Гостиная-кухня (пом. 1) |
| Дизайнер | Кырлан А.С. | | | 19.10.26 | |


| Стадия | Лист | Листов |
|---|---|---|
| П | 53 | 104 |

выпуск 19.10.2026 № 46d0102a0d · стр. 53 из 104

## Развёртка стены А

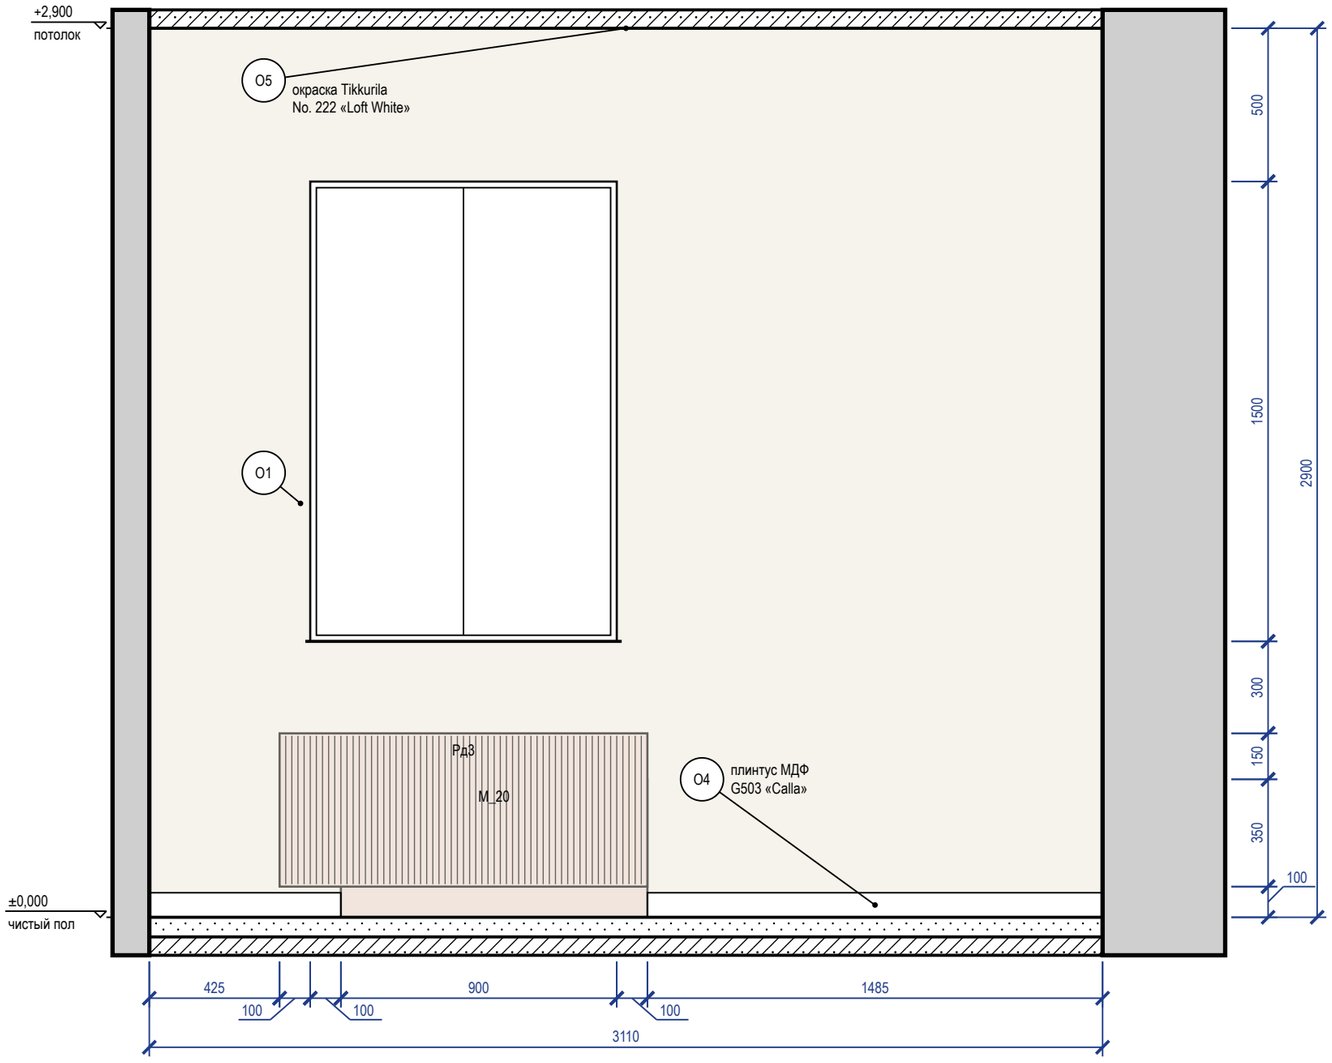


## Схема развёрток (М 1:100)

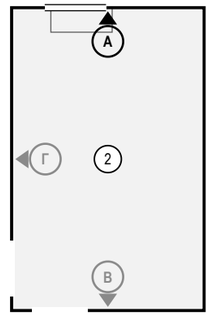


## Ведомость отделки (на листе)

| Марка | Поверхность | Материал, изделие | Цвет, код | Кол. |
|---|---|---|---|---|
| О1 | стены | окраска, Farrow & Ball Modern Emulsion, матовая, подготовка Q3 | Tikkurila G503 «Calla» | 7,5 м² |
| О4 | плинтус | плинтус МДФ, h 80 мм, аналог: плинтус МДФ под покраску 80×16 | Tikkurila G503 «Calla» | 2,1 м |
| О5 | потолок | окраска, Tikkurila Anti-Reflex 2, глубокоматовая, подготовка Q3 | Little Greene No. 222 «Loft White» | 15,5 м² |

## Примечания


1. Размеры — в мм от чистовых поверхностей стен; условные обозначения и общие указания — лист 2.

| | | | | | |
|---|---|---|---|---|---|
| | Лист | № док. | Подпись | Дата | Проект: Дом 120 м² |
| Дизайнер | Кырлан А.С. | | | 19.10.26 | Развёртка стены А. Холл с лестницей (пом. 2) |


| Стадия | Лист | Листов |
|---|---|---|
| П | 54 | 104 |

выпуск 19.10.2026 № 46d0102a0d · стр. 54 из 104

## Развёртка стены В

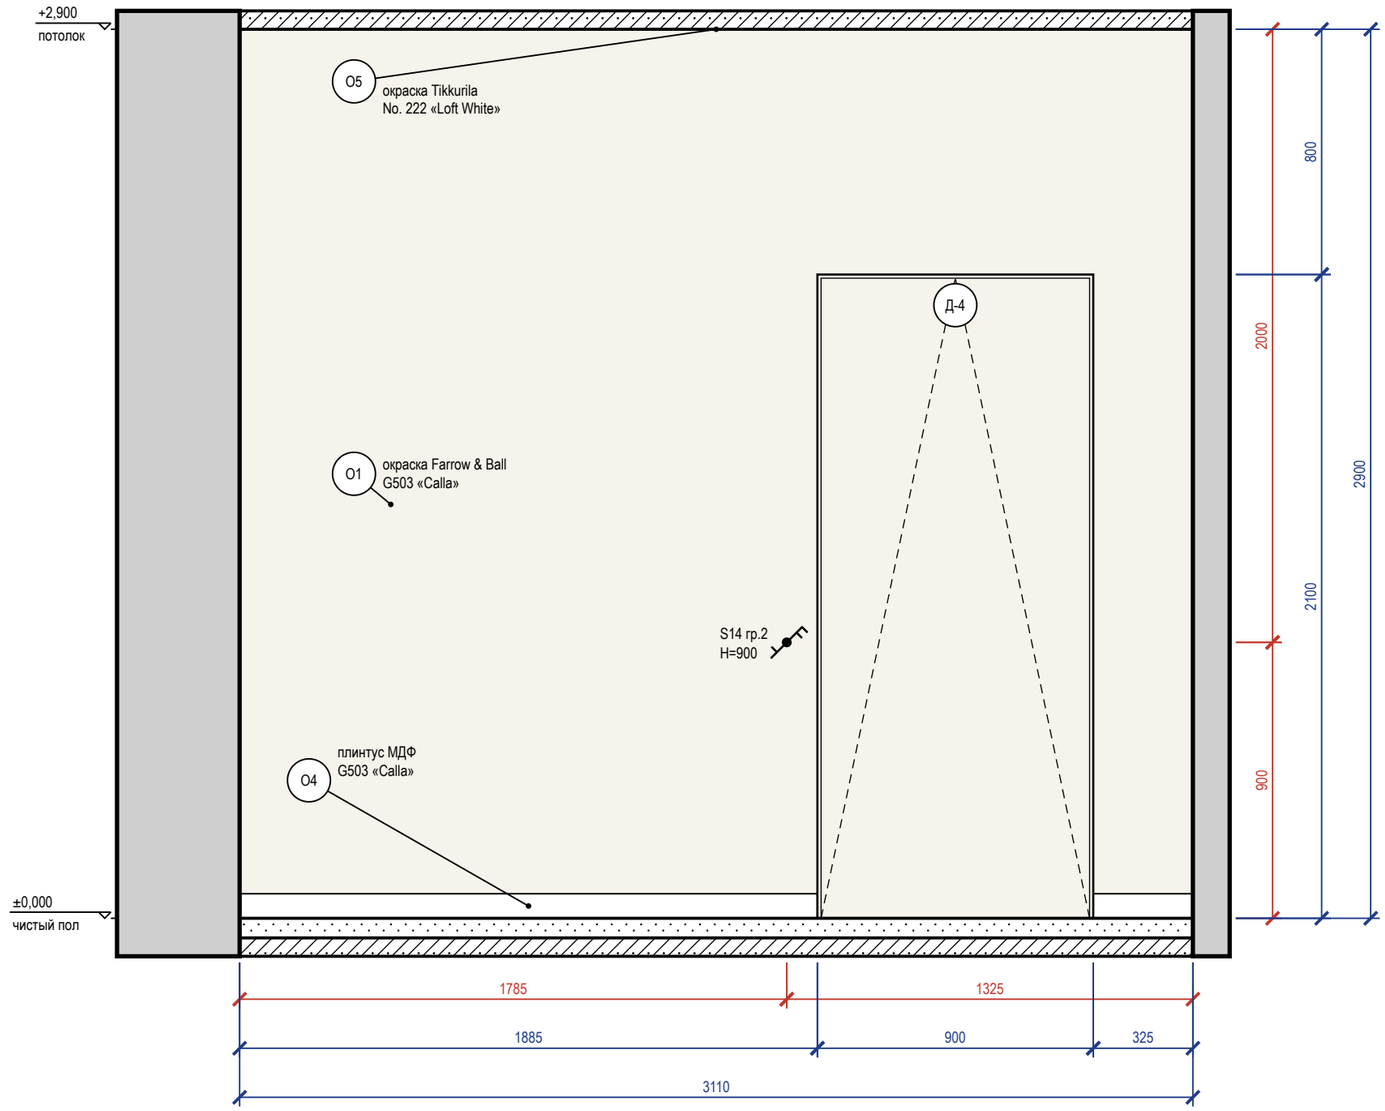


## Схема развёрток (М 1:100)

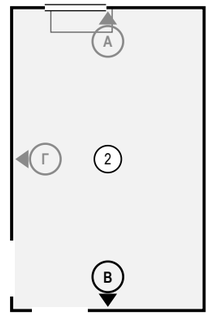


## Ведомость отделки (на листе)

| Марка | Поверхность | Материал, изделие | Цвет, код | Кол. |
|---|---|---|---|---|
| О1 | стены | окраска, Farrow & Ball Modern Emulsion, матовая, подготовка Q3 | Tikkurila G503 «Calla» | 7,1 м² |
| О4 | плинтус | плинтус МДФ, h 80 мм, аналог: плинтус МДФ под покраску 80×16 | Tikkurila G503 «Calla» | 2,2 м |
| О5 | потолок | окраска, Tikkurila Anti-Reflex 2, глубокоматовая, подготовка Q3 | Little Greene No. 222 «Loft White» | 15,5 м² |

## Примечания


1. Размеры — в мм от чистовых поверхностей стен; условные обозначения и общие указания — лист 2.
2. Двери скрытого монтажа — полотно в плоскости стены, отделка стены по полотну, плинтус прерывается у короба (узел — на листе узлов).

| | | | | | |
|---|---|---|---|---|---|
| | | | | | Проект: Дом 120 м² |
| | Лист | № док. | Подпись | Дата | Развёртка стены В. Холл с лестницей (пом. 2) |
| Дизайнер | Кырлан А.С. | | | 19.10.26 | |


| Стадия | Лист | Листов |
|---|---|---|
| П | 55 | 104 |

выпуск 19.10.2026 № 46d0102a0d · стр. 55 из 104

## Развёртка стены Г

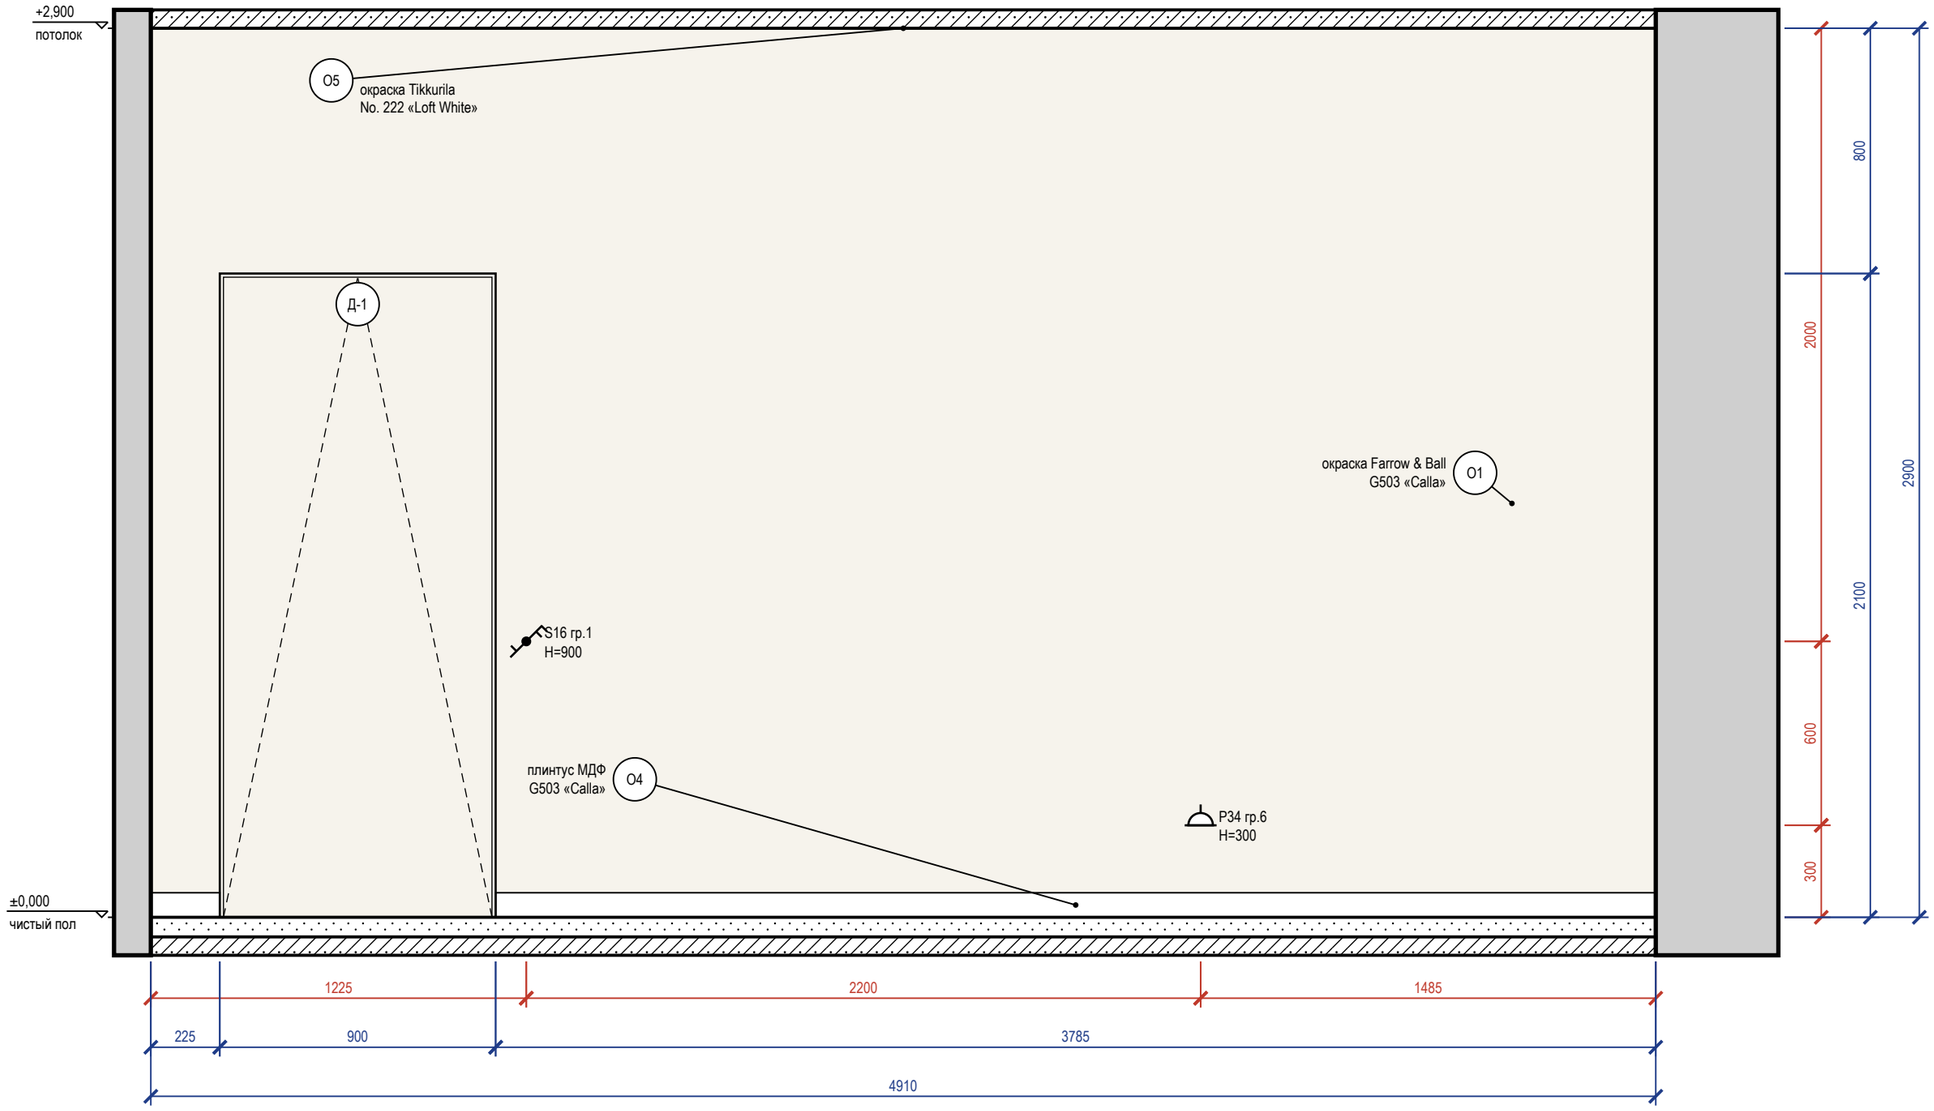


### Схема развёрток (М 1:100)

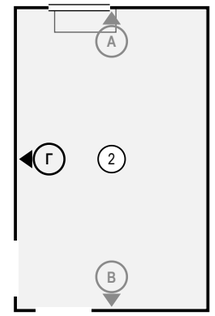


### Ведомость отделки (на листе)

| Марка | Поверхность | Материал, изделие | Цвет, код | Кол. |
|---|---|---|---|---|
| О1 | стены | окраска, Farrow & Ball Modern Emulsion, матовая, подготовка Q3 | Tikkurila G503 «Calla» | 12,3 м² |
| О4 | плинтус | плинтус МДФ, h 80 мм, аналог: плинтус МДФ под покраску 80×16 | Tikkurila G503 «Calla» | 4 м |
| О5 | потолок | окраска, Tikkurila Anti-Reflex 2, глубокоматовая, подготовка Q3 | Little Greene No. 222 «Loft White» | 15,5 м² |

### Примечания


1. Размеры — в мм от чистовых поверхностей стен; условные обозначения и общие указания — лист 2.
2. Двери скрытого монтажа — полотно в плоскости стены, отделка стены по полотну, плинтус прерывается у короба (узел — на листе узлов).

| | | | | | |
|---|---|---|---|---|---|
| | | | | | Проект: Дом 120 м² |
| | Лист | № док. | Подпись | Дата | Развёртка стены Г. Холл с лестницей (пом. 2) |
| Дизайнер | Кырлан А.С. | | | 19.10.26 | |


| Стадия | Лист | Листов |
|---|---|---|
| П | 56 | 104 |

выпуск 19.10.2026 № 46d0102a0d · стр. 56 из 104

## Развёртка стены А

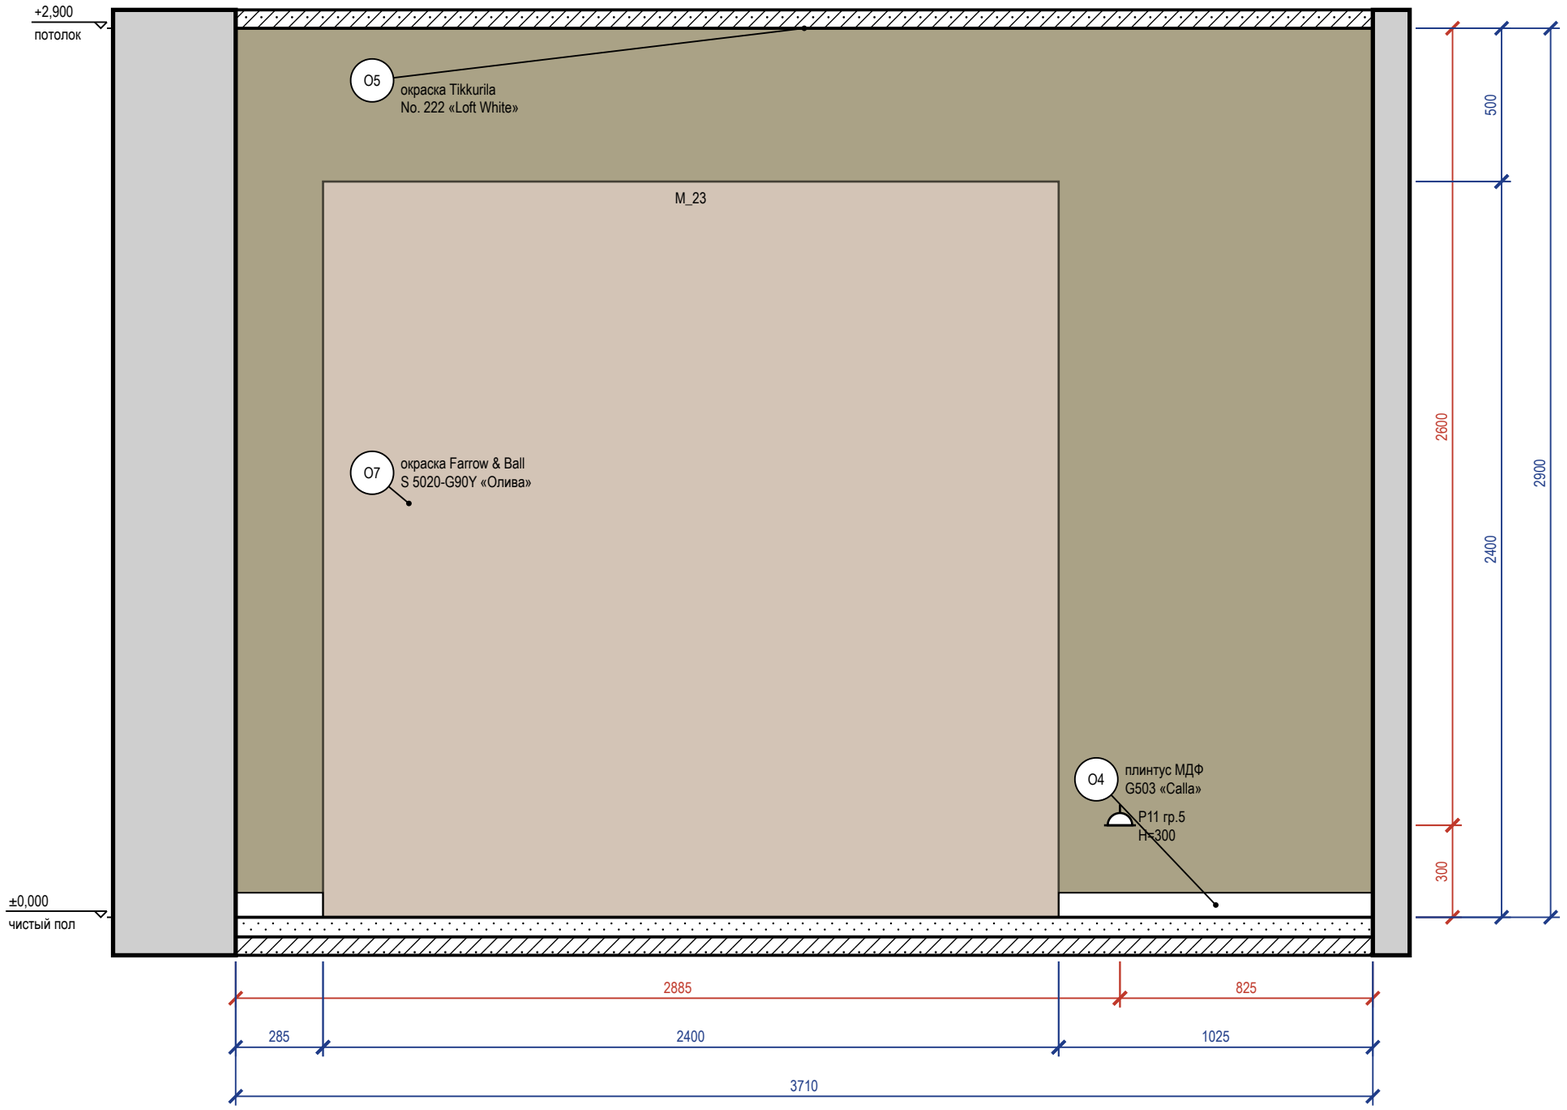


## Схема развёрток (М 1:100)

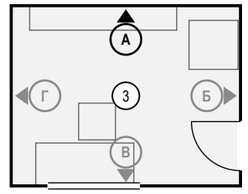


## Ведомость отделки (на листе)

| Марка | Поверхность | Материал, изделие | Цвет, код | Кол. |
|---|---|---|---|---|
| О4 | плинтус | плинтус МДФ, h 80 мм, аналог: плинтус МДФ под покраску 80×16 | Tikkurila G503 «Calla» | 1,3 м |
| О5 | потолок | окраска, Tikkurila Anti-Reflex 2, глубокоматовая, подготовка Q3 | Little Greene No. 222 «Loft White» | 11 м² |
| О7 | акцентная стена | окраска, Farrow & Ball Modern Emulsion, матовая, подготовка Q3 | NCS S 5020-G90Y «Олива» | 10,8 м² |

## Примечания


1. Размеры — в мм от чистовых поверхностей стен; условные обозначения и общие указания — лист 2.

| | | | | | |
|---|---|---|---|---|---|
| | Лист | № док. | Подпись | Дата | Проект: Дом 120 м² |
| Дизайнер | Кырлан А.С. | | | 19.10.26 | Развёртка стены А. Кабинет (пом. 3) |


| Стадия | Лист | Листов |
|---|---|---|
| П | 57 | 104 |

выпуск 19.10.2026 № 46d0102a0d · стр. 57 из 104

## Развёртка стены Б

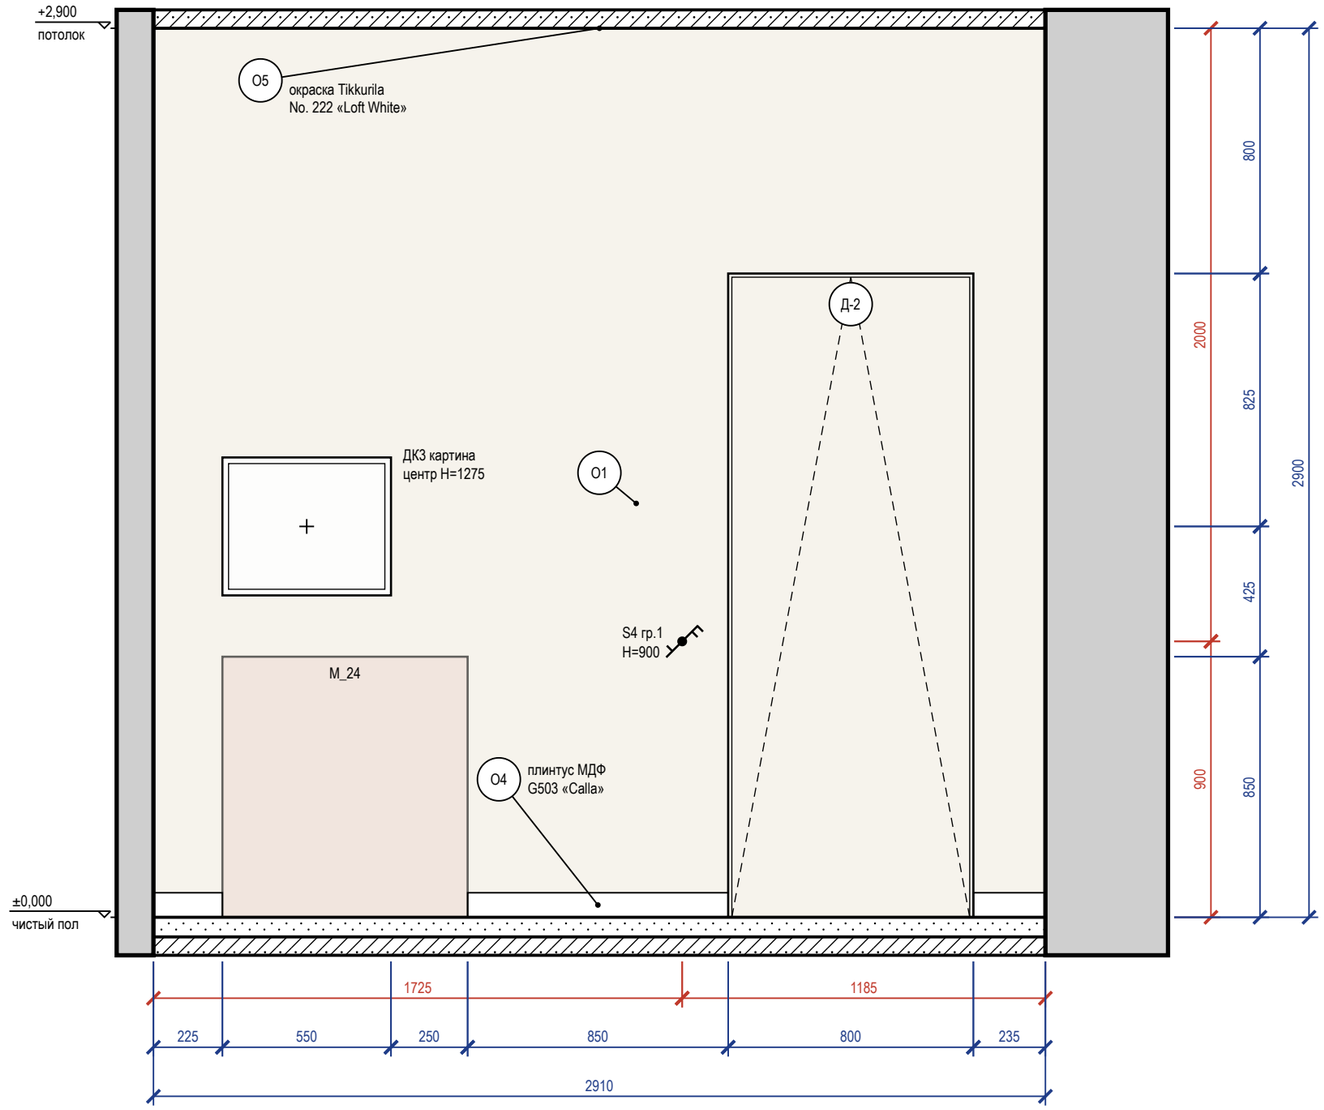


## Схема развёрток (М 1:100)

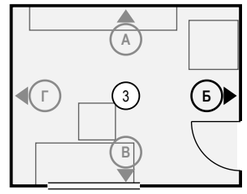


## Ведомость отделки (на листе)

| Марка | Поверхность | Материал, изделие | Цвет, код | Кол. |
|---|---|---|---|---|
| О1 | стены | окраска, Farrow & Ball Modern Emulsion, матовая, подготовка Q3 | Tikkurila G503 «Calla» | 6,8 м² |
| О4 | плинтус | плинтус МДФ, h 80 мм, аналог: плинтус МДФ под покраску 80×16 | Tikkurila G503 «Calla» | 1,3 м |
| О5 | потолок | окраска, Tikkurila Anti-Reflex 2, глубокоматовая, подготовка Q3 | Little Greene No. 222 «Loft White» | 11 м² |

## Примечания

1. Размеры — в мм от чистовых поверхностей стен; условные обозначения и общие указания — лист 2.
2. Картины и зеркала крепить к основанию по паспорту изделия (закладные и анкеры — в перечне скрытых работ); крест — ось центра предмета.
3. Двери скрытого монтажа — полотно в плоскости стены, отделка стены по полотну, плинтус прерывается у короба (узел — на листе узлов).

| | Лист | № док. | Подпись | Дата |
|---|---|---|---|---|
| Дизайнер | Кырлан А.С. | | | 19.10.26 |


Проект: Дом 120 м²

Развёртка стены Б. Кабинет (пом. 3)


| Стадия | Лист | Листов |
|---|---|---|
| П | 58 | 104 |

выпуск 19.10.2026 № 46d0102a0d · стр. 58 из 104

## Развёртка стены В

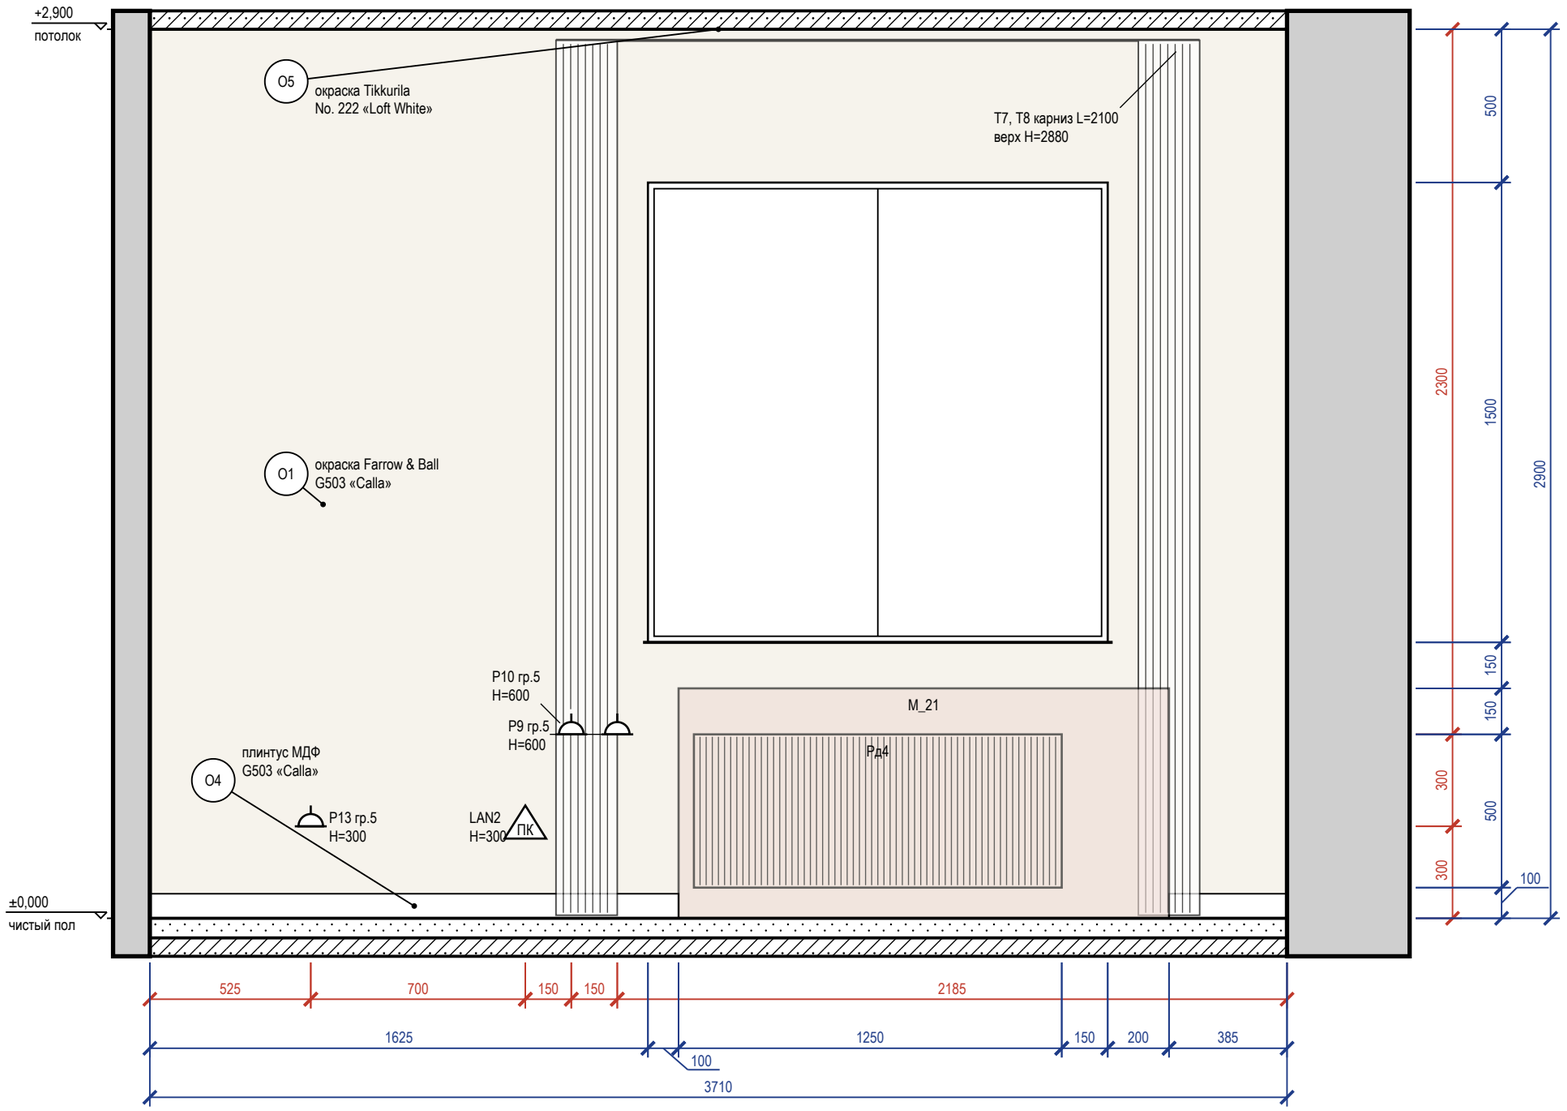


## Схема развёрток (М 1:100)

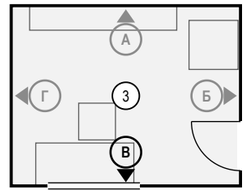


## Ведомость отделки (на листе)

| Марка | Поверхность | Материал, изделие | Цвет, код | Кол. |
|---|---|---|---|---|
| О1 | стены | окраска, Farrow & Ball Modern Emulsion, матовая, подготовка Q3 | Tikkurila G503 «Calla» | 8,5 м² |
| О4 | плинтус | плинтус МДФ, h 80 мм, аналог: плинтус МДФ под покраску 80×16 | Tikkurila G503 «Calla» | 2,1 м |
| О5 | потолок | окраска, Tikkurila Anti-Reflex 2, глубокоматовая, подготовка Q3 | Little Greene No. 222 «Loft White» | 11 м² |

## Примечания


1. Размеры — в мм от чистовых поверхностей стен; условные обозначения и общие указания — лист 2.
2. Карнизы (шины) — по ведомости текстиля декоратора; длина L и верх H — по развёртке, крепление — до окраски потолка.
3. Линии узора (швы плитки, складки штор, рёбра радиаторов) прерываются у знаков и выносок — просвет между линиями не менее 0,7 мм.

| | | | | | |
|---|---|---|---|---|---|
| | | | | | Проект: Дом 120 м² |
| | Лист | № док. | Подпись | Дата | Развёртка стены В. Кабинет (пом. 3) |
| Дизайнер | Кырлан А.С. | | | 19.10.26 | |


| Стадия | Лист | Листов |
|---|---|---|
| П | 59 | 104 |

выпуск 19.10.2026 № 46d0102a0d · стр. 59 из 104

## Развёртка стены Г

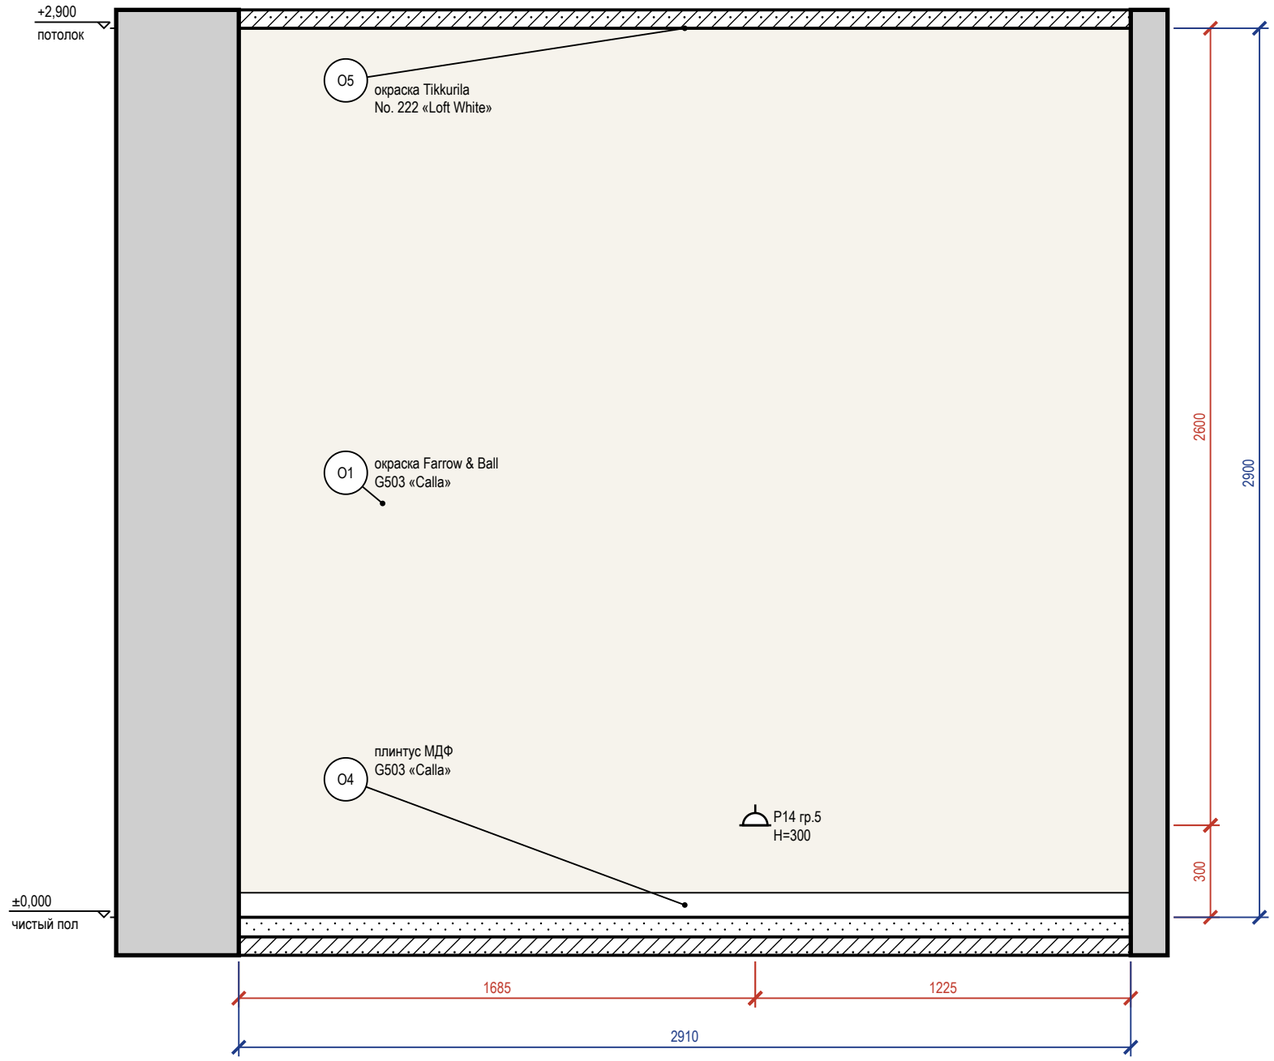


## Схема развёрток (М 1:100)

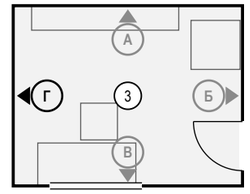


## Ведомость отделки (на листе)

| Марка | Поверхность | Материал, изделие | Цвет, код | Кол. |
|---|---|---|---|---|
| О1 | стены | окраска, Farrow & Ball Modern Emulsion, матовая, подготовка Q3 | Tikkurila G503 «Calla» | 8,4 м² |
| О4 | плинтус | плинтус МДФ, h 80 мм, аналог: плинтус МДФ под покраску 80×16 | Tikkurila G503 «Calla» | 2,9 м |
| О5 | потолок | окраска, Tikkurila Anti-Reflex 2, глубокоматовая, подготовка Q3 | Little Greene No. 222 «Loft White» | 11 м² |

## Примечания


1. Размеры — в мм от чистовых поверхностей стен; условные обозначения и общие указания — лист 2.

| | | | | | |
|---|---|---|---|---|---|
| | | | | | Проект: Дом 120 м² |
| | Лист | № док. | Подпись | Дата | Развёртка стены Г. Кабинет (пом. 3) |
| Дизайнер | Кырлан А.С. | | | 19.10.26 | |


| Стадия | Лист | Листов |
|---|---|---|
| П | 60 | 104 |

выпуск 19.10.2026 № 46d0102a0d · стр. 60 из 104


## Развёртка стены А

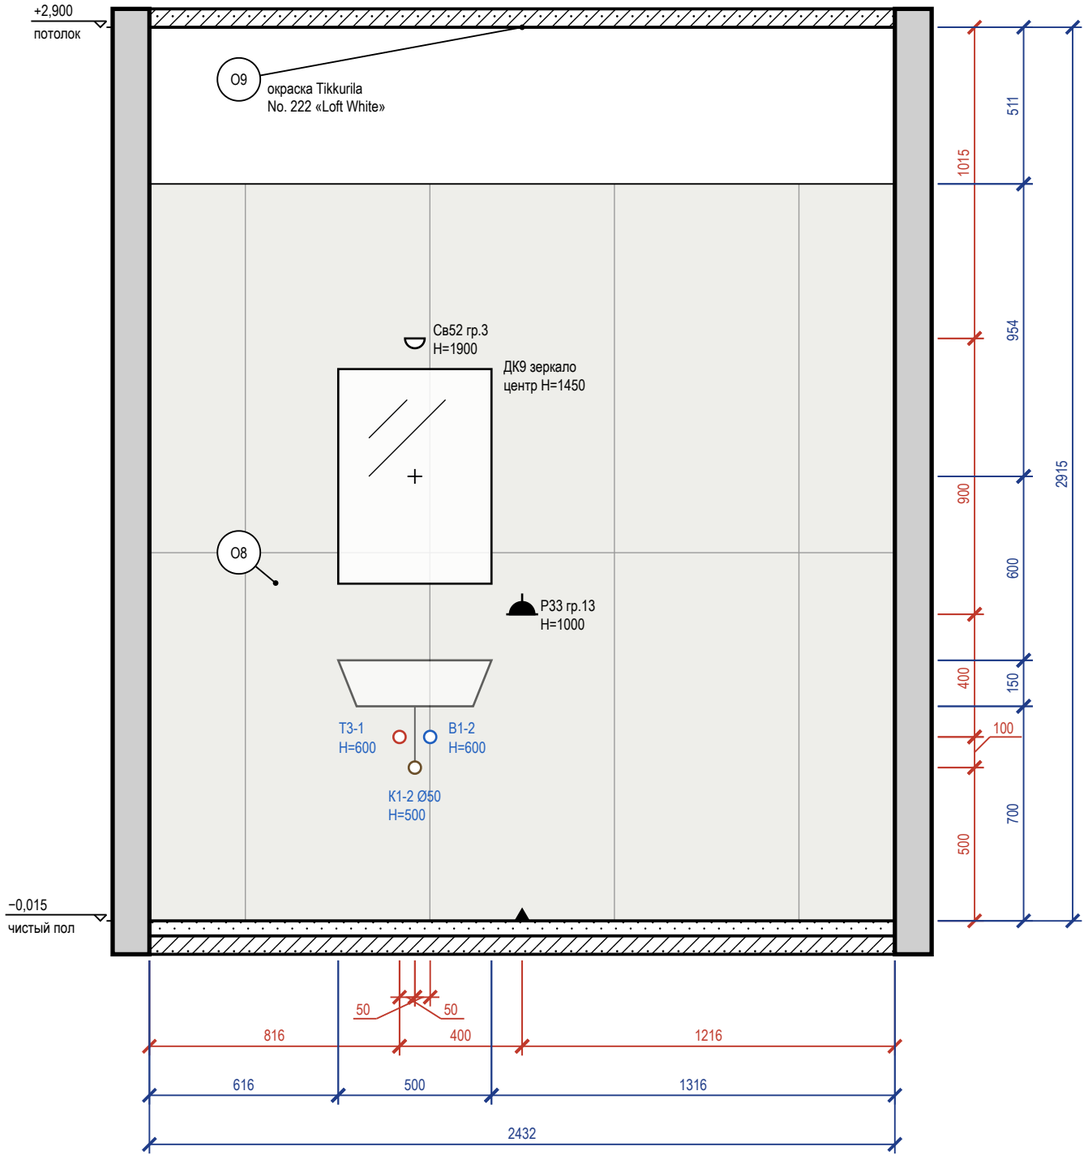


## Развёртка стены Б

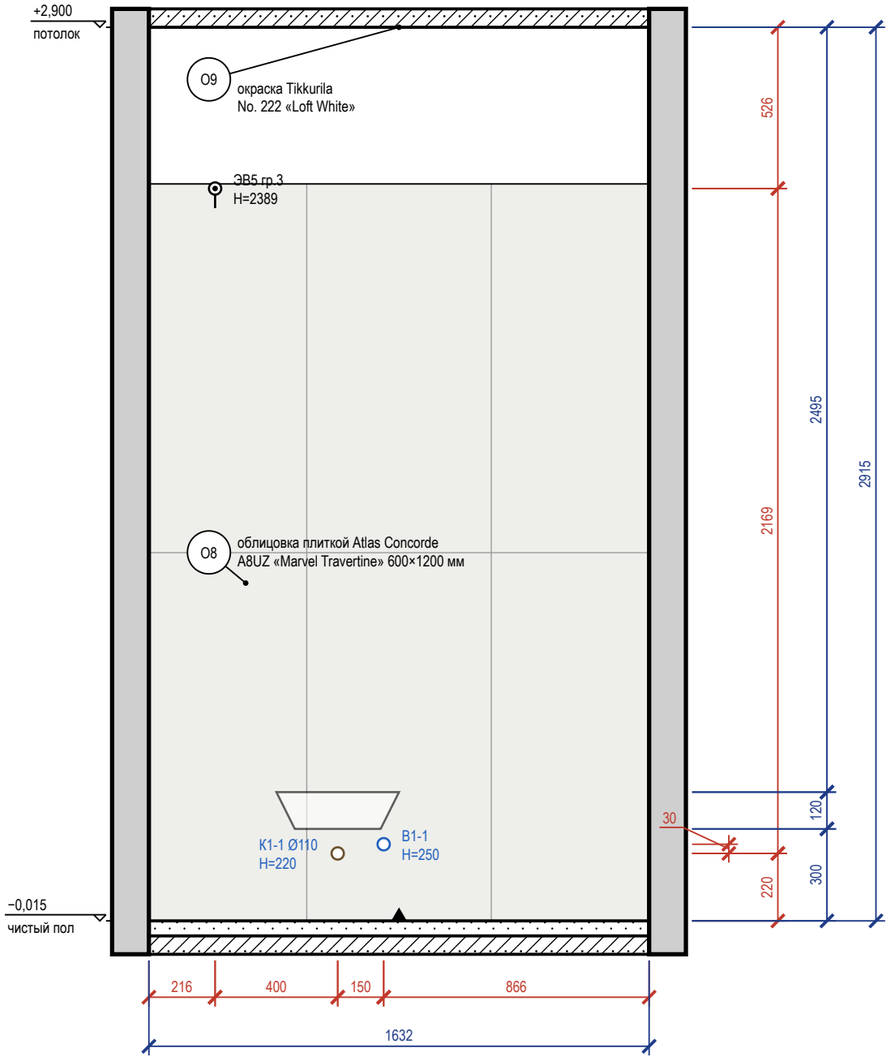


### Схема развёрток (М 1:100)

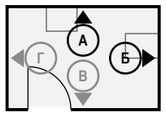


### Ведомость отделки (на листе)

| Марка | Поверхность | Материал, изделие | Цвет, код | Кол. |
|---|---|---|---|---|
| О8 | стены | облицовка плиткой, Atlas Concorde Marvel Travertine, 600×1200×9 мм, A8UZ, затирка CG2WA | Atlas Concorde A8UZ «Marvel Travertine» | 9,8 м² |
| О9 | потолок | окраска, Tikkurila Luja 7, матовая, подготовка Q3 | Little Greene No. 222 «Loft White» | 4,2 м² |

### Примечания


1. Размеры — в мм от чистовых поверхностей стен; условные обозначения и общие указания — лист 2.
2. Схема мебели, приборов и декора не является технической документацией для производства мебели; габариты — по паспортам изделий.
3. Выводы ВК — коды и высоты по листу выводов сантехники.
4. Облицовка — по сетке швов 2 мм, раскладка от оси стены (треугольник у пола), целые ряды от пола; подрезки — по листу раскладки плитки.
5. Гидроизоляция в 2 слоя, заход на стены 200 мм — до облицовки, с актом скрытых работ и тестом проливом (узел — на листе узлов).
6. Картины и зеркала крепить к основанию по паспорту изделия (закладные и анкеры — в перечне скрытых работ); крест — ось центра предмета.

| | | | | | |
|---|---|---|---|---|---|
| | | | | | Проект: Дом 120 м² |
| | Лист | № док. | Подпись | Дата | Развёртки стен А, Б. Санузел гостевой (пом. 4) |
| Дизайнер | Кырлан А.С. | | | 19.10.26 | |


| Стадия | Лист | Листов |
|---|---|---|
| П | 61 | 104 |

выпуск 19.10.2026 № 46d0102a0d · стр. 61 из 104


## Развёртка стены В

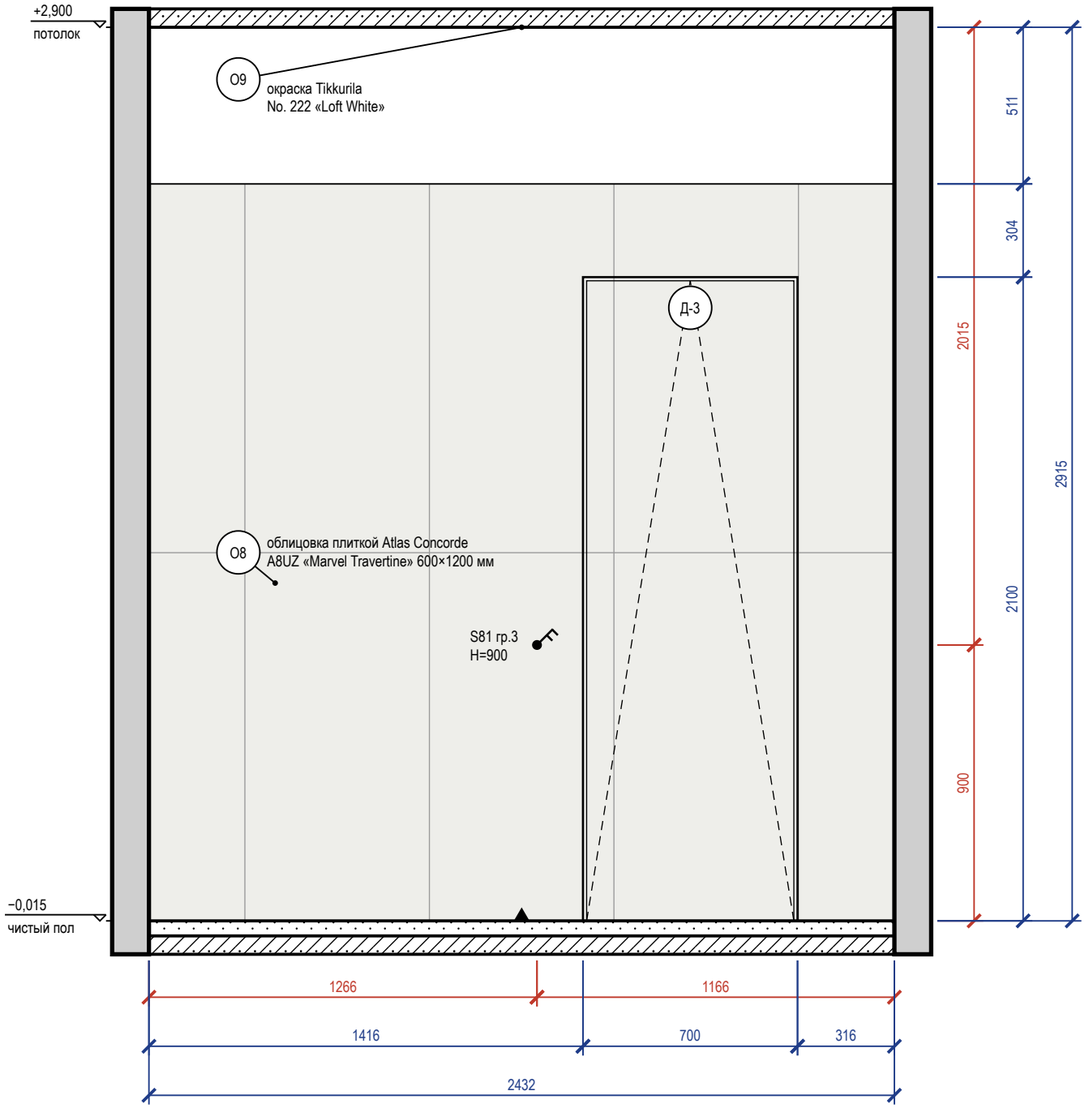


## Развёртка стены Г

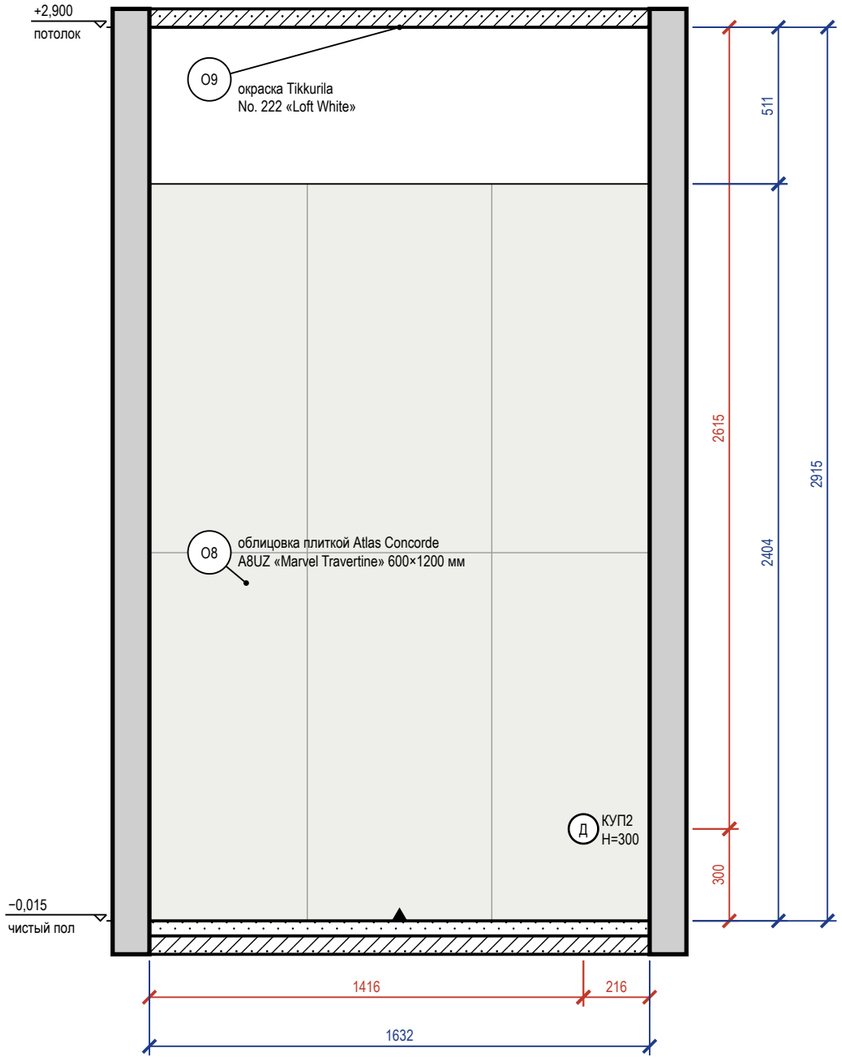


### Схема развёрток (М 1:100)

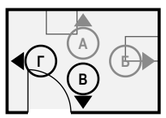


### Ведомость отделки (на листе)

| Марка | Поверхность | Материал, изделие | Цвет, код | Кол. |
|---|---|---|---|---|
| О8 | стены | облицовка плиткой, Atlas Concorde Marvel Travertine, 600×1200×9 мм, A8UZ, затирка CG2WA | Atlas Concorde A8UZ «Marvel Travertine» | 8,3 м² |
| О9 | потолок | окраска, Tikkurila Luja 7, матовая, подготовка Q3 | Little Greene No. 222 «Loft White» | 4,2 м² |

### Примечания


1. Размеры — в мм от чистовых поверхностей стен; условные обозначения и общие указания — лист 2.
2. Облицовка — по сетке швов 2 мм, раскладка от оси стены (треугольник у пола), целые ряды от пола; подрезки — по листу раскладки плитки.
3. Гидроизоляция в 2 слоя, заход на стены 200 мм — до облицовки, с актом скрытых работ и тестом проливом (узел — на листе узлов).
4. Двери скрытого монтажа — полотно в плоскости стены, отделка стены по полотну, плинтус прерывается у короба (узел — на листе узлов).

| | | | | | |
|---|---|---|---|---|---|
| | | | | | Проект: Дом 120 м² |
| | Лист | № док. | Подпись | Дата | Развёртки стен В, Г. Санузел гостевой (пом. 4) |
| Дизайнер | Кырлан А.С. | | | 19.10.26 | |


| Стадия | Лист | Листов |
|---|---|---|
| П | 62 | 104 |

выпуск 19.10.2026 № 46d0102a0d · стр. 62 из 104

## Развёртка стены А1

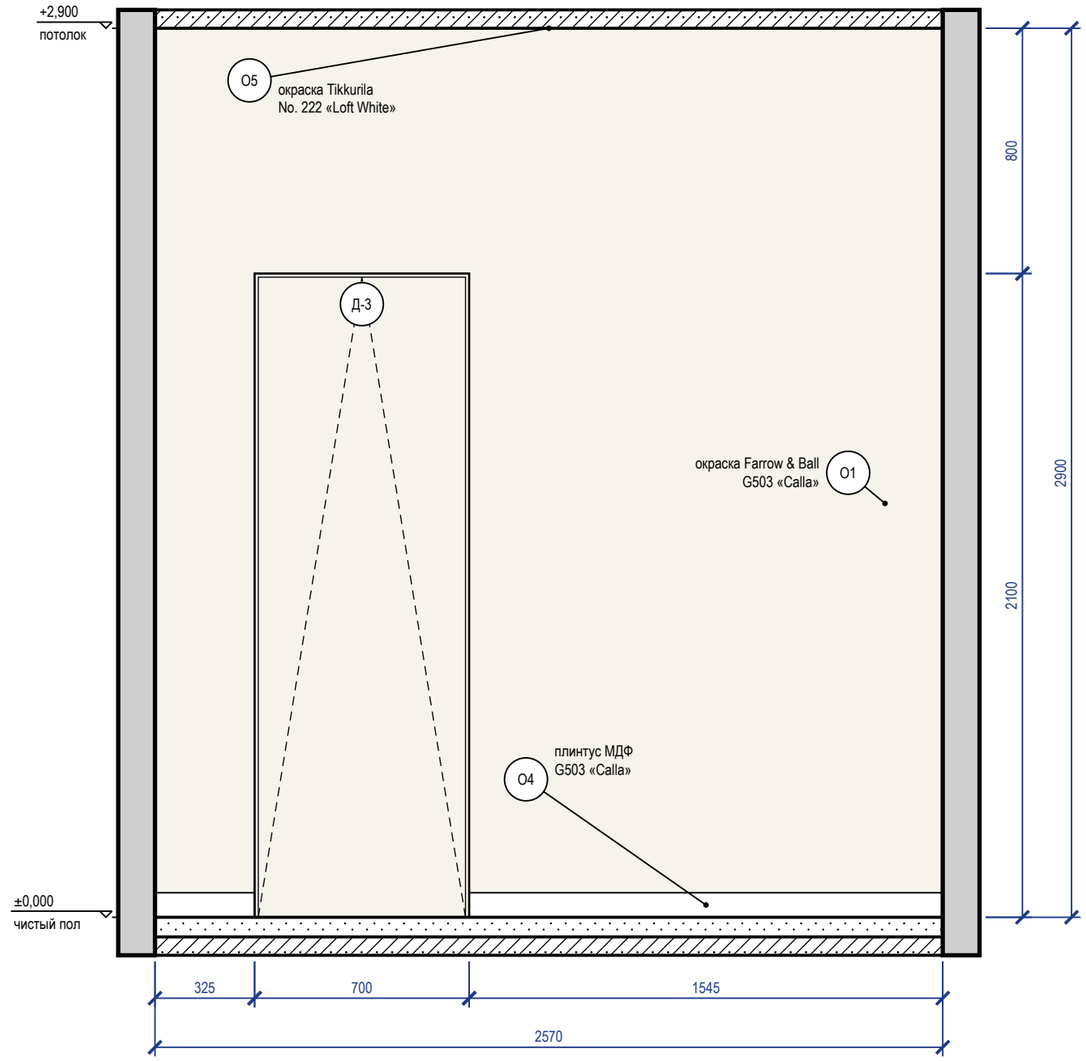


## Схема развёрток (М 1:100)

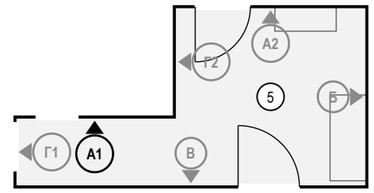


## Ведомость отделки (на листе)

| Марка | Поверхность | Материал, изделие | Цвет, код | Кол. |
|---|---|---|---|---|
| О1 | стены | окраска, Farrow & Ball Modern Emulsion, матовая, подготовка Q3 | Tikkurila G503 «Calla» | 6 м² |
| О4 | плинтус | плинтус МДФ, h 80 мм, аналог: плинтус МДФ под покраску 80×16 | Tikkurila G503 «Calla» | 1,9 м |
| О5 | потолок | окраска, Tikkurila Anti-Reflex 2, глубокоматовая, подготовка Q3 | Little Greene No. 222 «Loft White» | 12,2 м² |

## Примечания


1. Размеры — в мм от чистовых поверхностей стен; условные обозначения и общие указания — лист 2.
2. Двери скрытого монтажа — полотно в плоскости стены, отделка стены по полотну, плинтус прерывается у короба (узел — на листе узлов).

| | | | | | |
|---|---|---|---|---|---|
| | | | | | Проект: Дом 120 м² |
| | Лист | № док. | Подпись | Дата | Развёртка стены А1. Прихожая (пом. 5) |
| Дизайнер | Кырлан А.С. | | | 19.10.26 | |


| Стадия | Лист | Листов |
|---|---|---|
| П | 63 | 104 |

выпуск 19.10.2026 № 46d0102a0d · стр. 63 из 104

## Развёртка стены А2

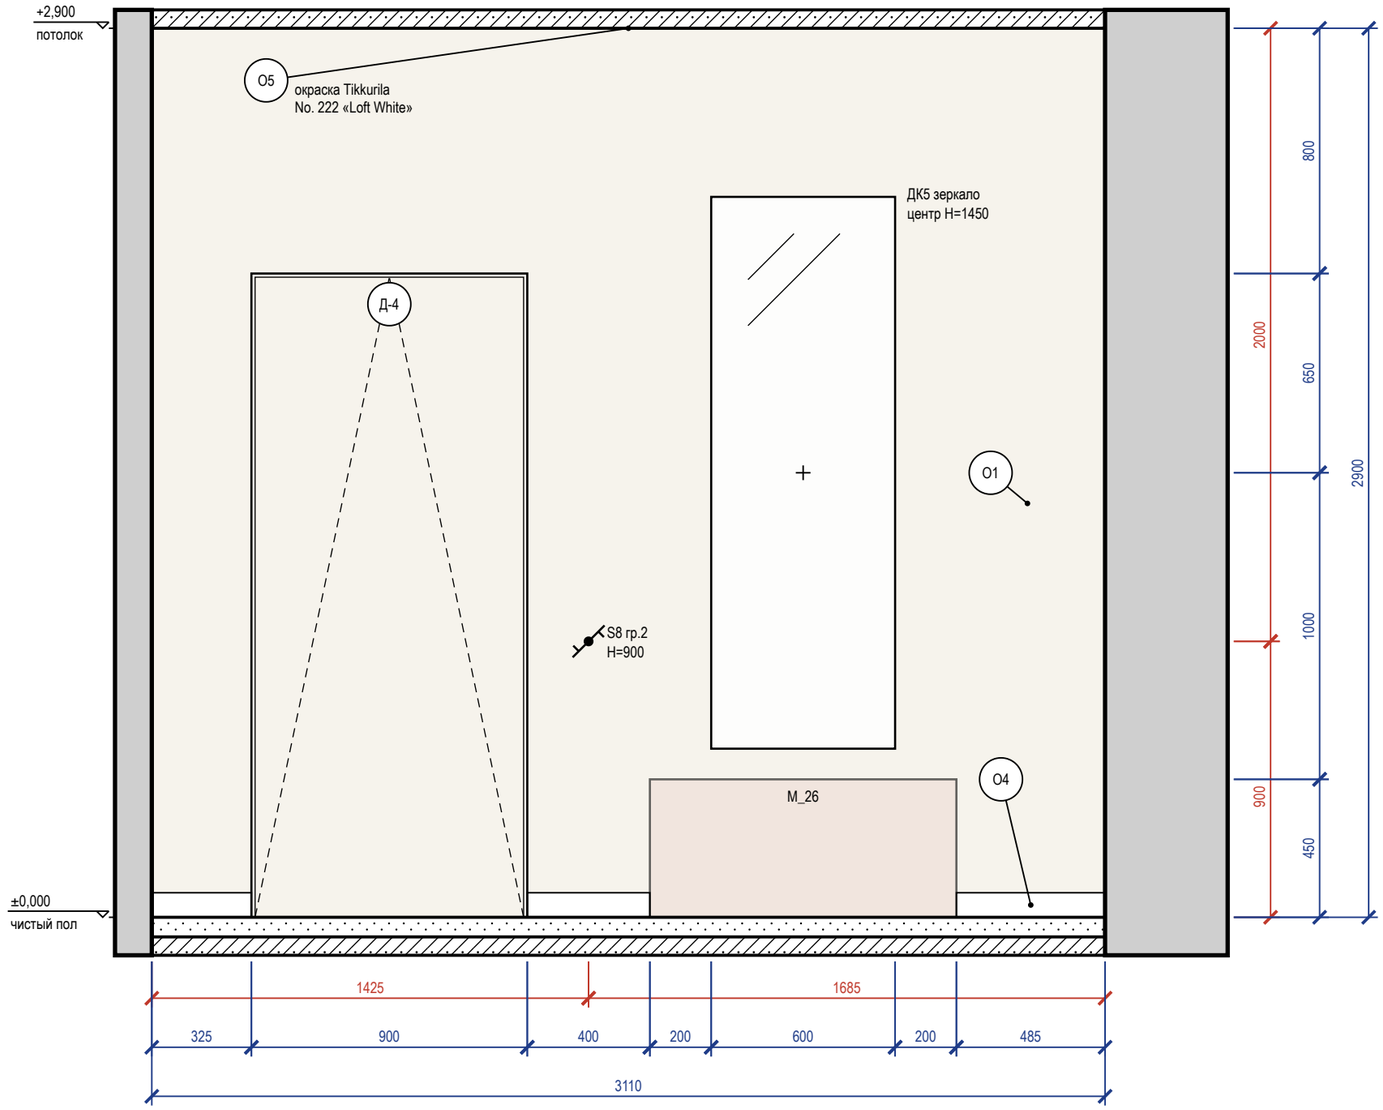


## Схема развёрток (М 1:100)

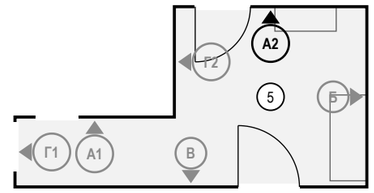


## Ведомость отделки (на листе)

| Марка | Поверхность | Материал, изделие | Цвет, код | Кол. |
|---|---|---|---|---|
| О1 | стены | окраска, Farrow & Ball Modern Emulsion, матовая, подготовка Q3 | Tikkurila G503 «Calla» | 7,1 м² |
| О4 | плинтус | плинтус МДФ, h 80 мм, аналог: плинтус МДФ под покраску 80×16 | Tikkurila G503 «Calla» | 1,2 м |
| О5 | потолок | окраска, Tikkurila Anti-Reflex 2, глубокоматовая, подготовка Q3 | Little Greene No. 222 «Loft White» | 12,2 м² |

## Примечания

1. Размеры — в мм от чистовых поверхностей стен; условные обозначения и общие указания — лист 2.
2. Картины и зеркала крепить к основанию по паспорту изделия (закладные и анкеры — в перечне скрытых работ); крест — ось центра предмета.
3. Двери скрытого монтажа — полотно в плоскости стены, отделка стены по полотну, плинтус прерывается у короба (узел — на листе узлов).

| | Лист | № док. | Подпись | Дата |
|---|---|---|---|---|
| Дизайнер | Кырлан А.С. | | | 19.10.26 |


Проект: Дом 120 м²

Развёртка стены А2. Прихожая (пом. 5)


| Стадия | Лист | Листов |
|---|---|---|
| П | 64 | 104 |

выпуск 19.10.2026 № 46d0102a0d · стр. 64 из 104

## Развёртка стены Б

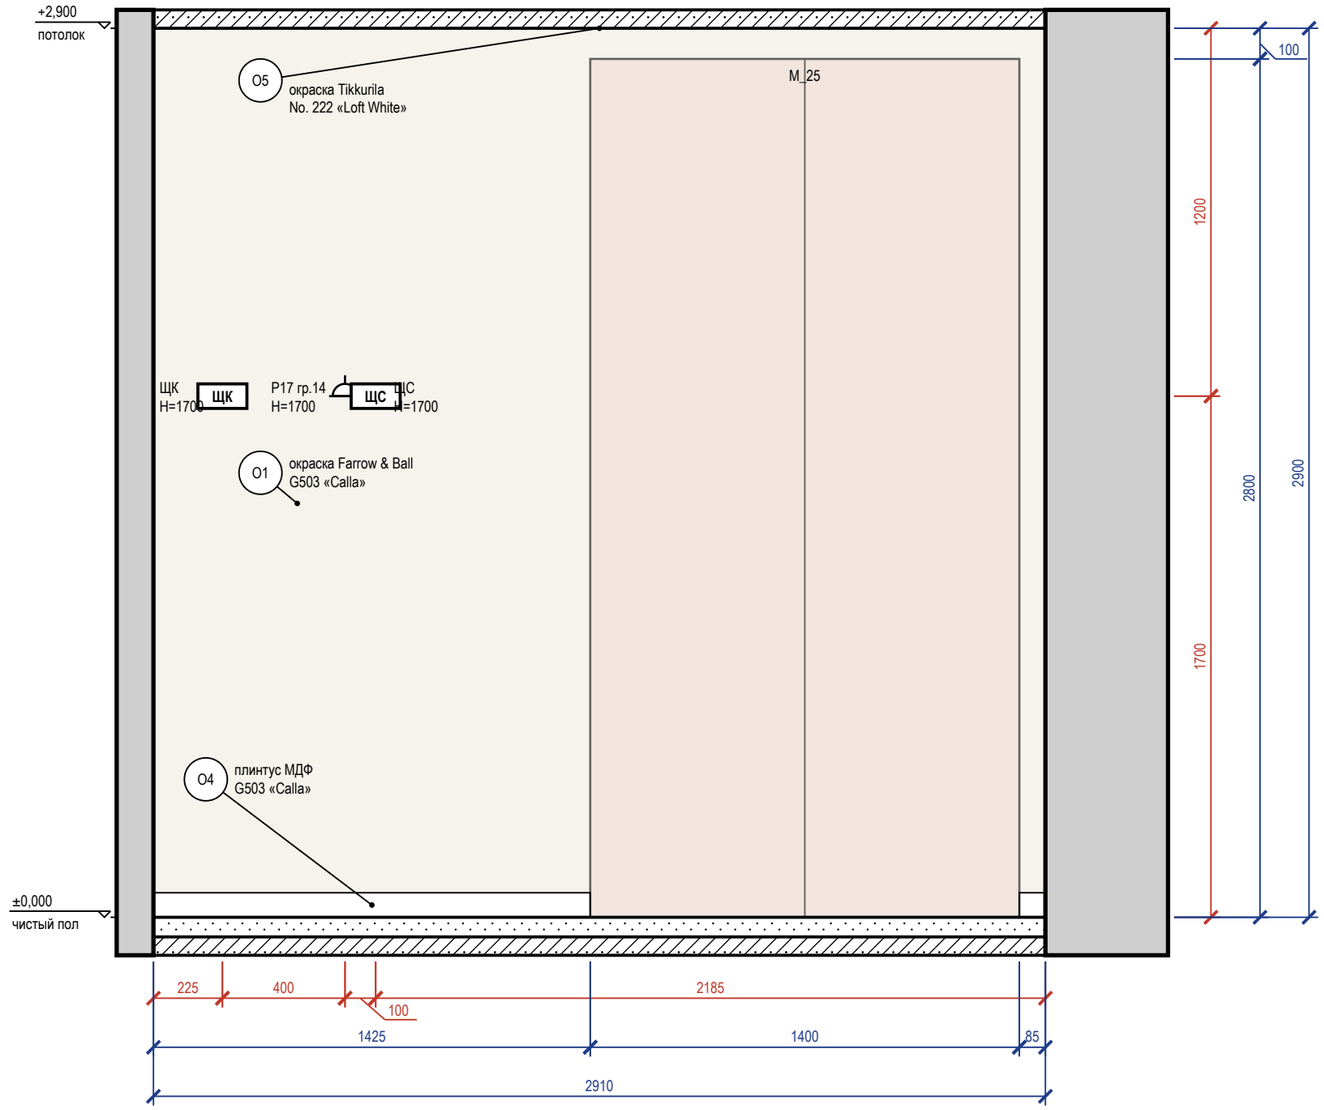


## Схема развёрток (М 1:100)

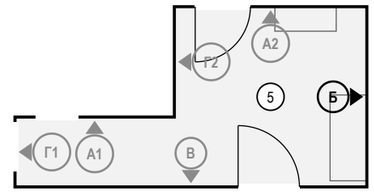


## Ведомость отделки (на листе)

| Марка | Поверхность | Материал, изделие | Цвет, код | Кол. |
|---|---|---|---|---|
| О1 | стены | окраска, Farrow & Ball Modern Emulsion, матовая, подготовка Q3 | Tikkurila G503 «Calla» | 8,4 м² |
| О4 | плинтус | плинтус МДФ, h 80 мм, аналог: плинтус МДФ под покраску 80×16 | Tikkurila G503 «Calla» | 1,5 м |
| О5 | потолок | окраска, Tikkurila Anti-Reflex 2, глубокоматовая, подготовка Q3 | Little Greene No. 222 «Loft White» | 12,2 м² |

## Примечания


1. Размеры — в мм от чистовых поверхностей стен; условные обозначения и общие указания — лист 2.

| | | | | | |
|---|---|---|---|---|---|
| | | | | | Проект: Дом 120 м² |
| | Лист | № док. | Подпись | Дата | Развёртка стены Б. Прихожая (пом. 5) |
| Дизайнер | Кырлан А.С. | | | 19.10.26 | |


| Стадия | Лист | Листов |
|---|---|---|
| П | 65 | 104 |

выпуск 19.10.2026 № 46d0102a0d · стр. 65 из 104

## Развёртка стены В

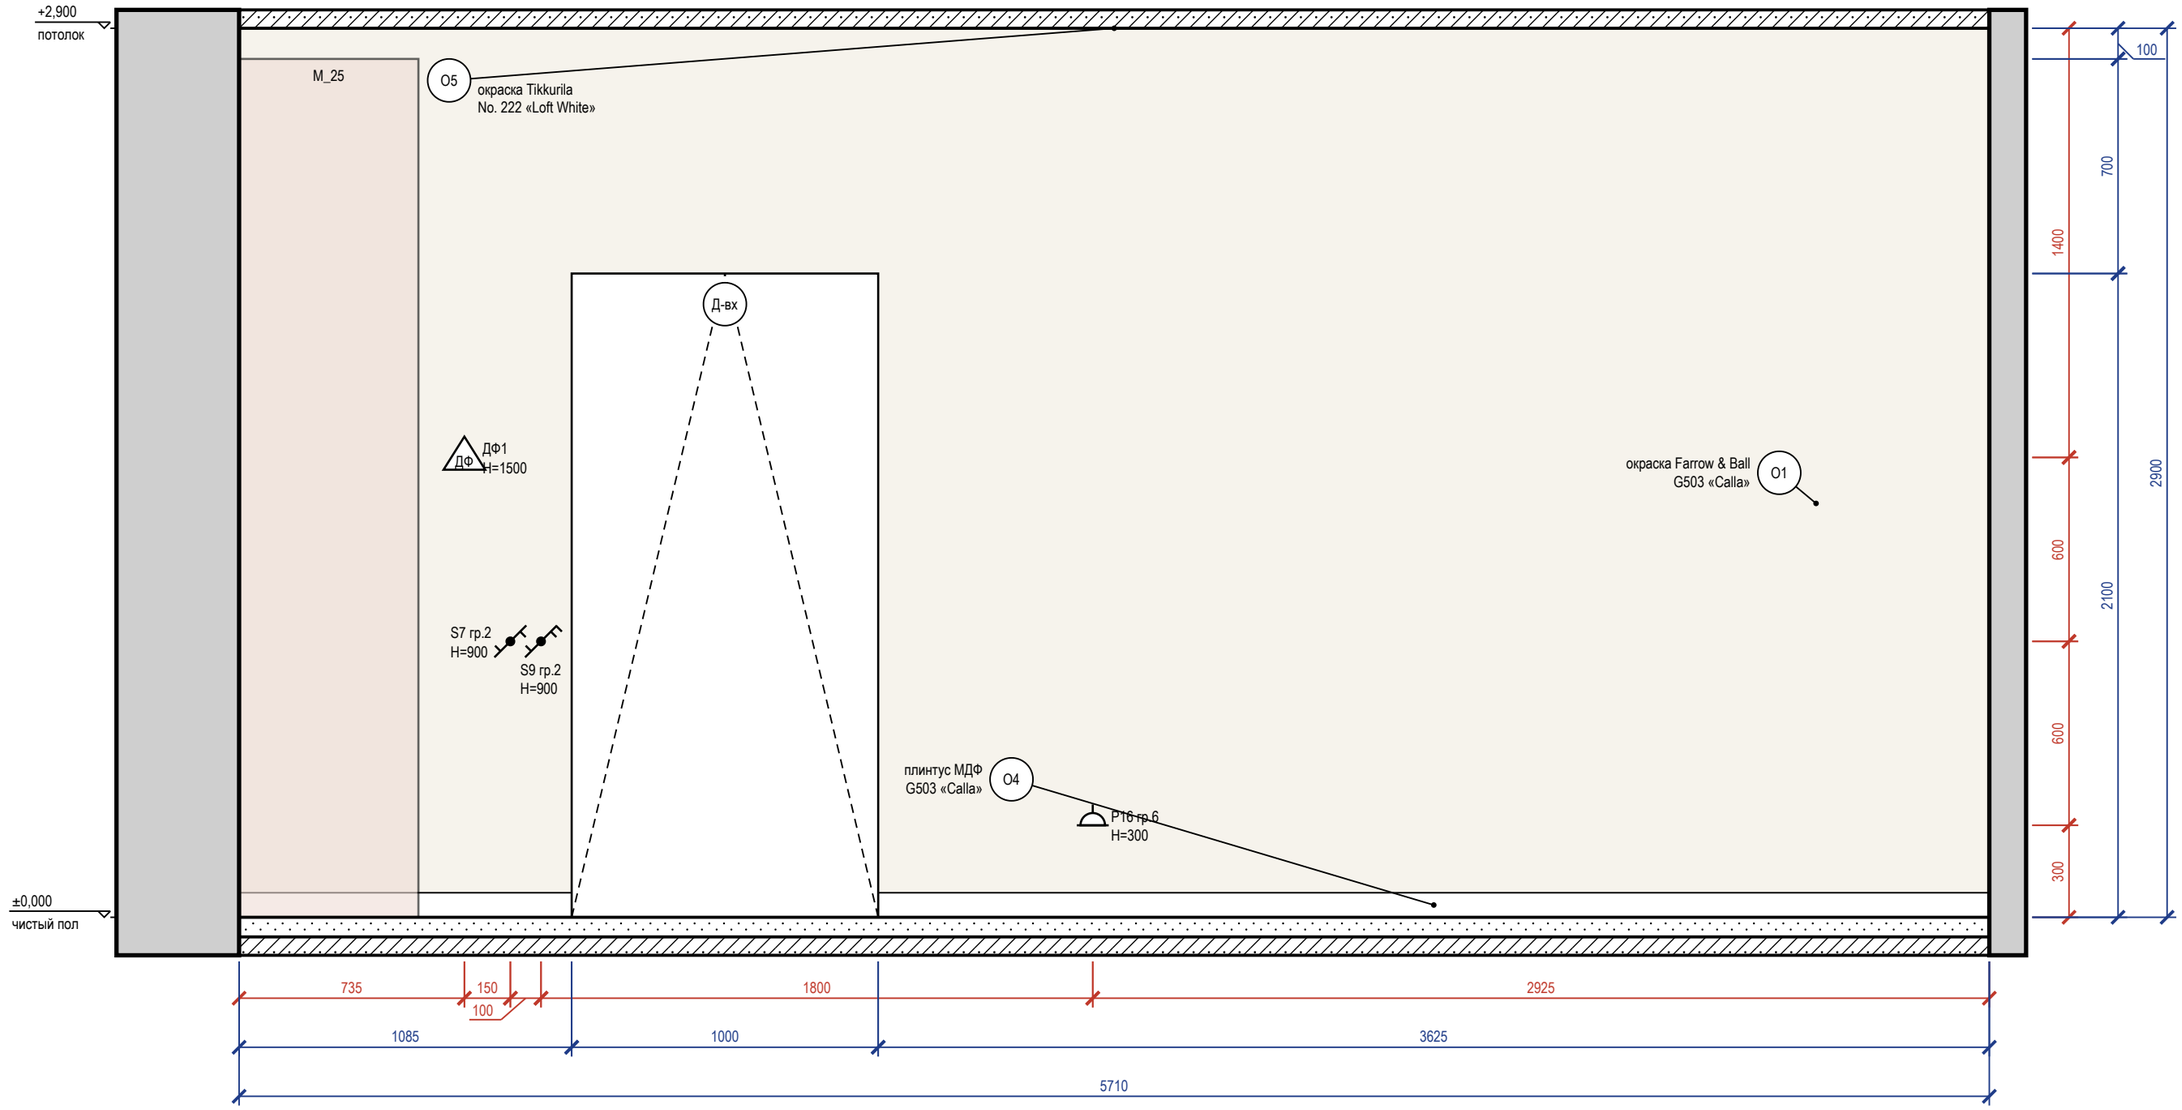


### Схема развёрток (М 1:100)

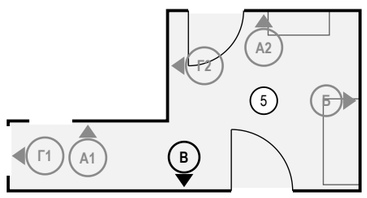


### Ведомость отделки (на листе)

| Марка | Поверхность | Материал, изделие | Цвет, код | Кол. |
|---|---|---|---|---|
| О1 | стены | окраска, Farrow & Ball Modern Emulsion, матовая, подготовка Q3 | Tikkurila G503 «Calla» | 14,5 м² |
| О4 | плинтус | плинтус МДФ, h 80 мм, аналог: плинтус МДФ под покраску 80×16 | Tikkurila G503 «Calla» | 4,7 м |
| О5 | потолок | окраска, Tikkurila Anti-Reflex 2, глубокоматовая, подготовка Q3 | Little Greene No. 222 «Loft White» | 12,2 м² |

### Примечания


1. Размеры — в мм от чистовых поверхностей стен; условные обозначения и общие указания — лист 2.

| | | | | | |
|---|---|---|---|---|---|
| | | | | | Проект: Дом 120 м² |
| | Лист | № док. | Подпись | Дата | Развёртка стены В. Прихожая (пом. 5) |
| Дизайнер | Кырлан А.С. | | | 19.10.26 | |


| Стадия | Лист | Листов |
|---|---|---|
| П | 66 | 104 |

выпуск 19.10.2026 № 46d0102a0d · стр. 66 из 104


## Развёртка стены Г1

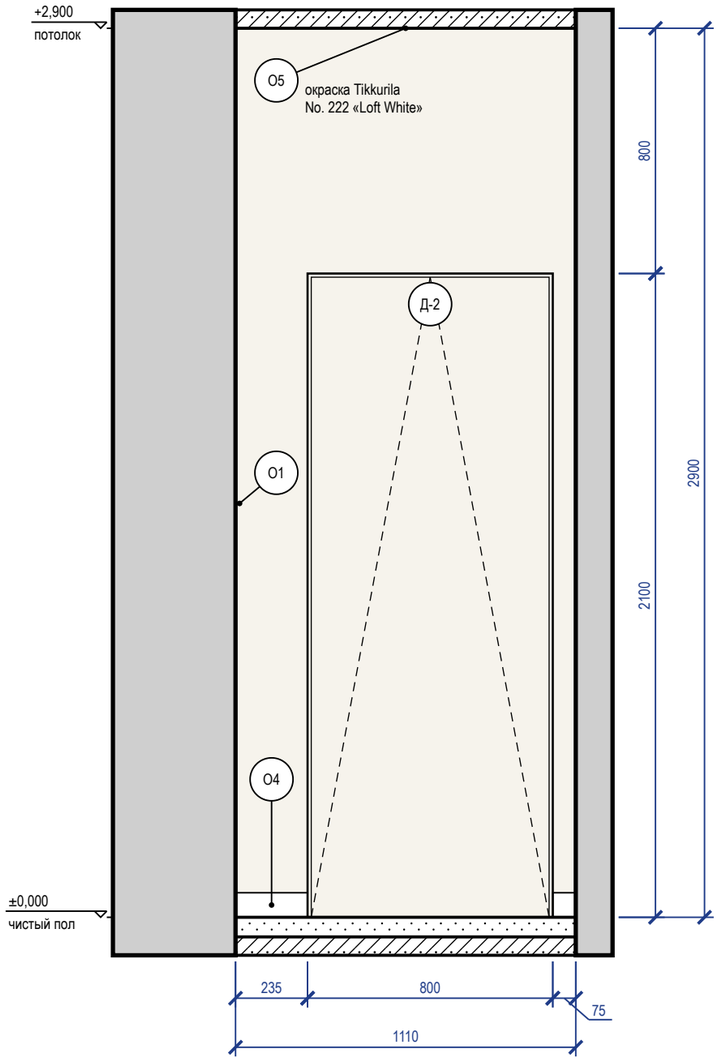


## Развёртка стены Г2

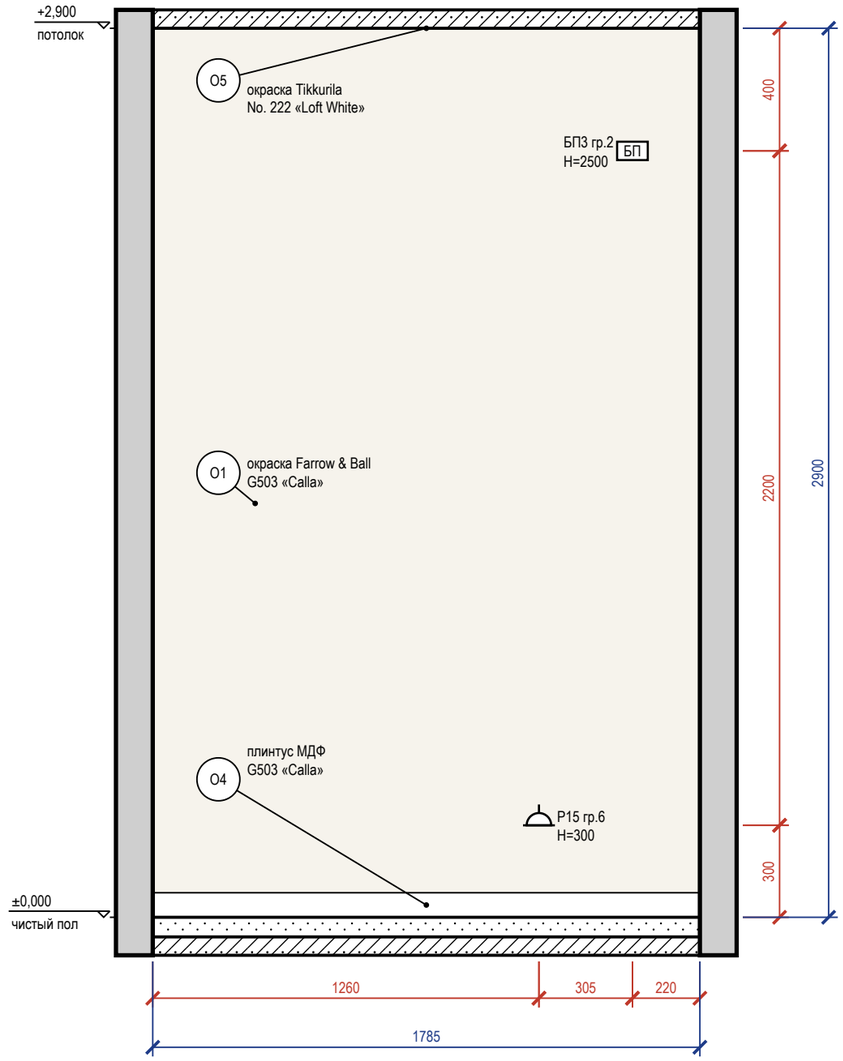


## Схема развёрток (М 1:100)

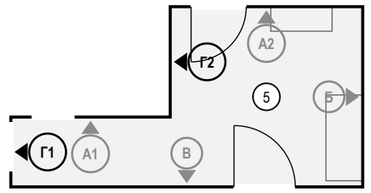


## Ведомость отделки (на листе)

| Марка | Поверхность | Материал, изделие | Цвет, код | Кол. |
|---|---|---|---|---|
| О1 | стены | окраска, Farrow & Ball Modern Emulsion, матовая, подготовка Q3 | Tikkurila G503 «Calla» | 6,7 м² |
| О4 | плинтус | плинтус МДФ, h 80 мм, аналог: плинтус МДФ под покраску 80×16 | Tikkurila G503 «Calla» | 2,1 м |
| О5 | потолок | окраска, Tikkurila Anti-Reflex 2, глубокоматовая, подготовка Q3 | Little Greene No. 222 «Loft White» | 12,2 м² |

## Примечания


1. Размеры — в мм от чистовых поверхностей стен; условные обозначения и общие указания — лист 2.
2. Двери скрытого монтажа — полотно в плоскости стены, отделка стены по полотну, плинтус прерывается у короба (узел — на листе узлов).

| | | | | | |
|---|---|---|---|---|---|
| | | | | | Проект: Дом 120 м² |
| | Лист | № док. | Подпись | Дата | Развёртки стен Г1, Г2. Прихожая (пом. 5) |
| Дизайнер | Кырлан А.С. | | | 19.10.26 | |


| Стадия | Лист | Листов |
|---|---|---|
| П | 67 | 104 |

выпуск 19.10.2026 № 46d0102a0d · стр. 67 из 104

## Развёртка стены А

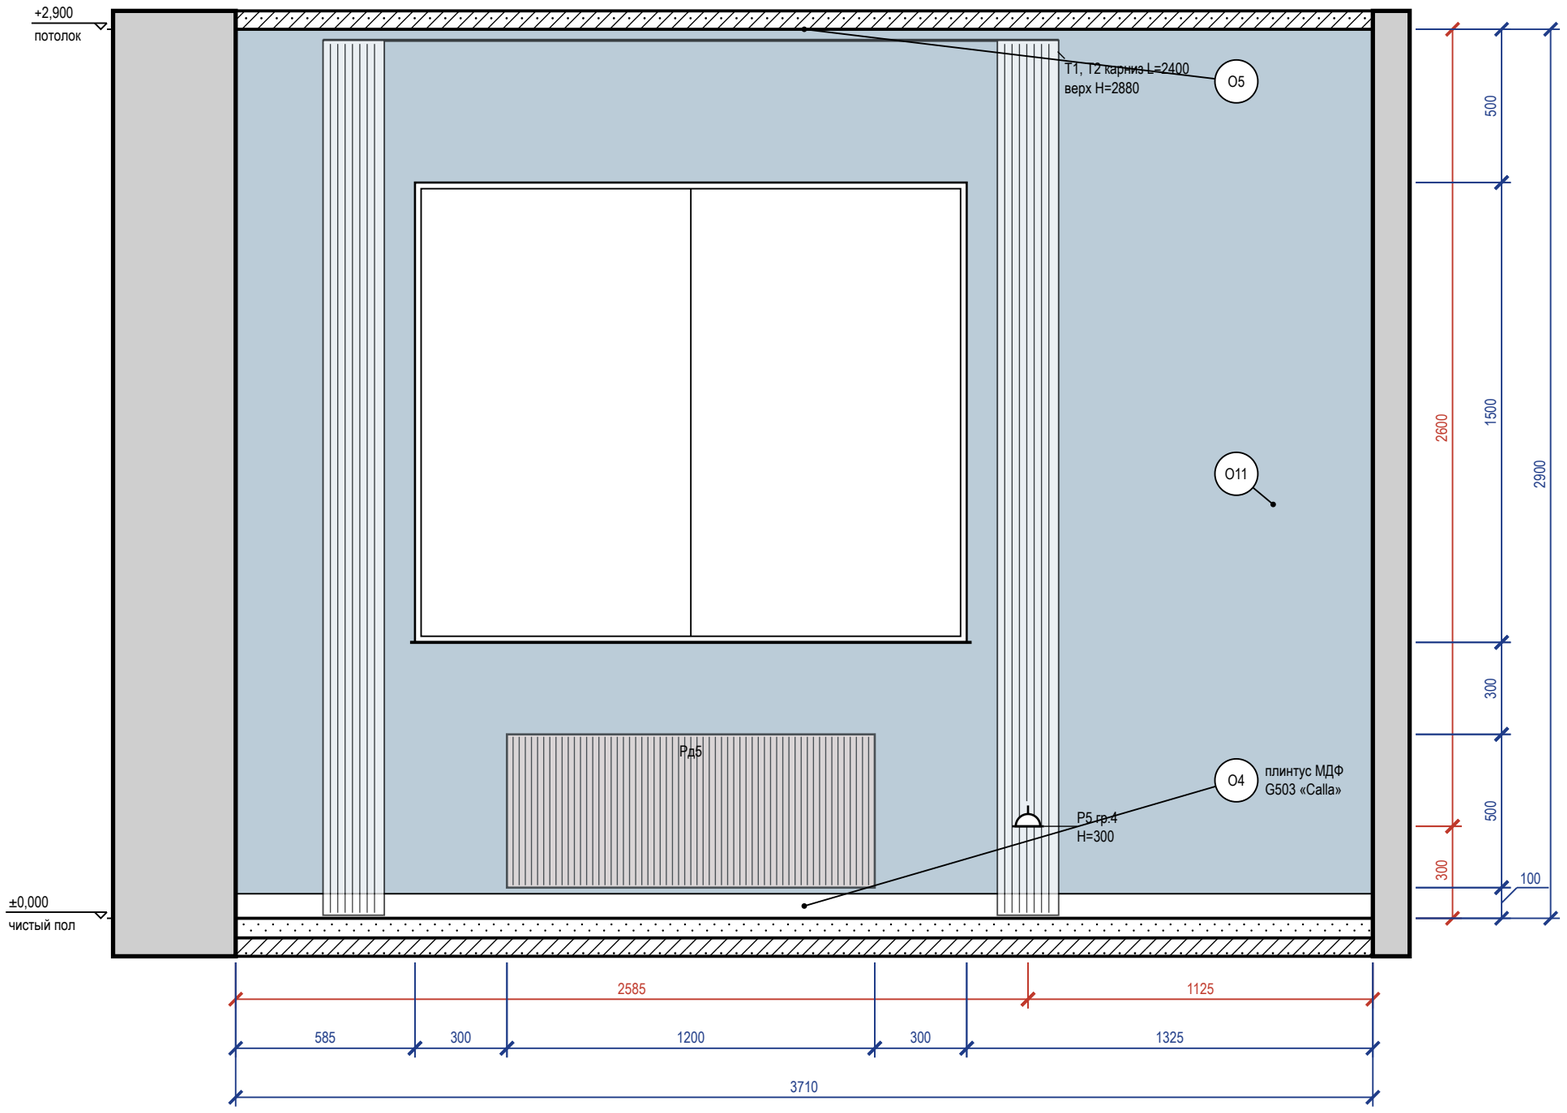


## Схема развёрток (М 1:100)

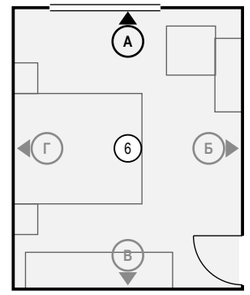


## Ведомость отделки (на листе)

| Марка | Поверхность | Материал, изделие | Цвет, код | Кол. |
|---|---|---|---|---|
| О4 | плинтус | плинтус МДФ, h 80 мм, аналог: плинтус МДФ под покраску 80×16 | Tikkurila G503 «Calla» | 3,7 м |
| О5 | потолок | окраска, Tikkurila Anti-Reflex 2, глубокоматовая, подготовка Q3 | Little Greene No. 222 «Loft White» | 17,2 м² |
| О11 | акцентная стена | окраска, Farrow & Ball Modern Emulsion, матовая, подготовка Q3 | Farrow & Ball No. 89 «Lulworth Blue — светлая морская лазурь» | 8,1 м² |

### Примечания


1. Размеры — в мм от чистовых поверхностей стен; условные обозначения и общие указания — лист 2.
2. Карнизы (шины) — по ведомости текстиля декоратора; длина L и верх H — по развёртке, крепление — до окраски потолка.
3. Линии узора (швы плитки, складки штор, рёбра радиаторов) прерываются у знаков и выносок — просвет между линиями не менее 0,7 мм.

| | | | | | |
|---|---|---|---|---|---|
| | | | | | Проект: Дом 120 м² |
| | Лист | № док. | Подпись | Дата | Развёртка стены А. Спальня родителей (пом. 6) |
| Дизайнер | Кырлан А.С. | | | 19.10.26 | |


| Стадия | Лист | Листов |
|---|---|---|
| П | 68 | 104 |

выпуск 19.10.2026 № 46d0102a0d · стр. 68 из 104

## Развёртка стены Б

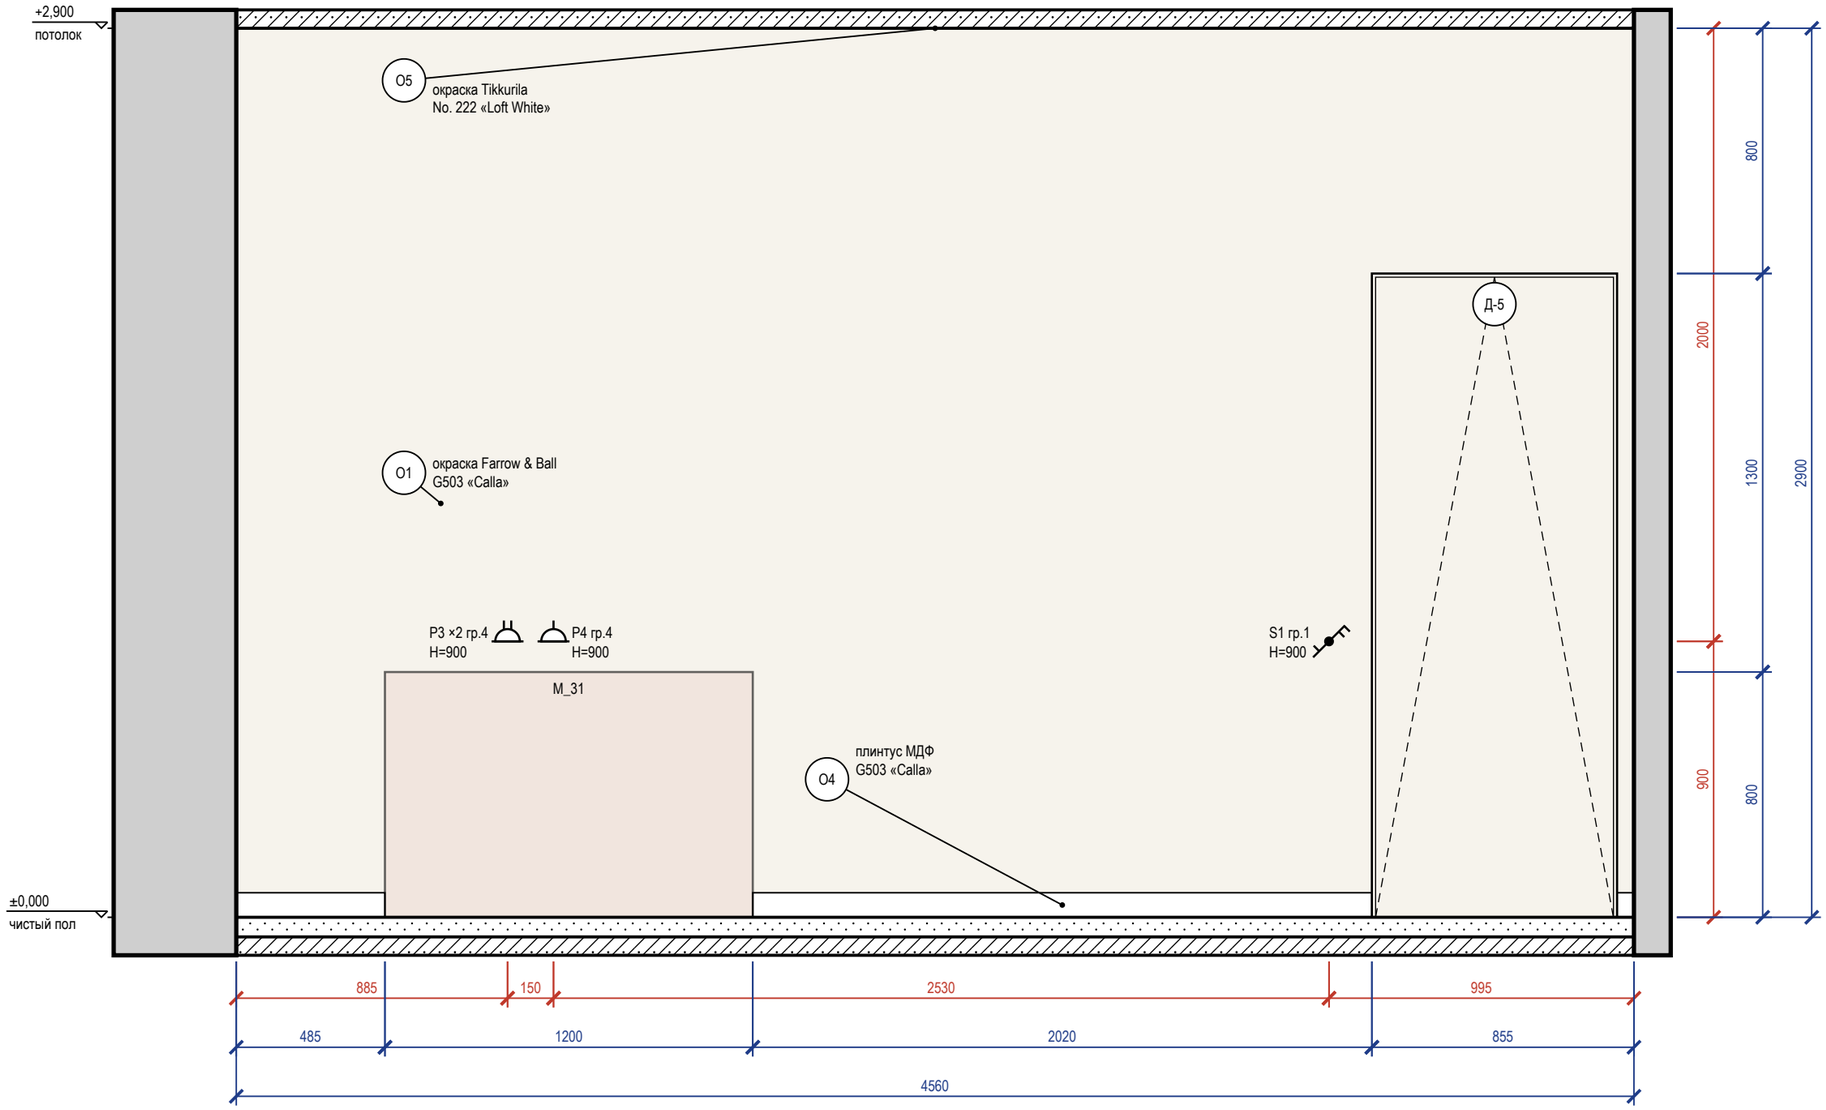


### Схема развёрток (М 1:100)

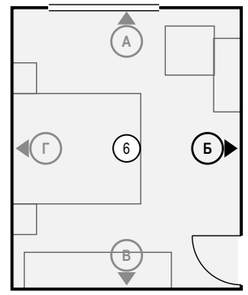


### Ведомость отделки (на листе)

| Марка | Поверхность | Материал, изделие | Цвет, код | Кол. |
|---|---|---|---|---|
| О1 | стены | окраска, Farrow & Ball Modern Emulsion, матовая, подготовка Q3 | Tikkurila G503 «Calla» | 11,5 м² |
| О4 | плинтус | плинтус МДФ, h 80 мм, аналог: плинтус МДФ под покраску 80×16 | Tikkurila G503 «Calla» | 2,6 м |
| О5 | потолок | окраска, Tikkurila Anti-Reflex 2, глубокоматовая, подготовка Q3 | Little Greene No. 222 «Loft White» | 17,2 м² |

### Примечания


1. Размеры — в мм от чистовых поверхностей стен; условные обозначения и общие указания — лист 2.
2. Двери скрытого монтажа — полотно в плоскости стены, отделка стены по полотну, плинтус прерывается у короба (узел — на листе узлов).

| | | | | | |
|---|---|---|---|---|---|
| | | | | | Проект: Дом 120 м² |
| | Лист | № док. | Подпись | Дата | Развёртка стены Б. Спальня родителей (пом. 6) |
| Дизайнер | Кырлан А.С. | | | 19.10.26 | |


| Стадия | Лист | Листов |
|---|---|---|
| П | 69 | 104 |

выпуск 19.10.2026 № 46d0102a0d · стр. 69 из 104

## Развёртка стены В

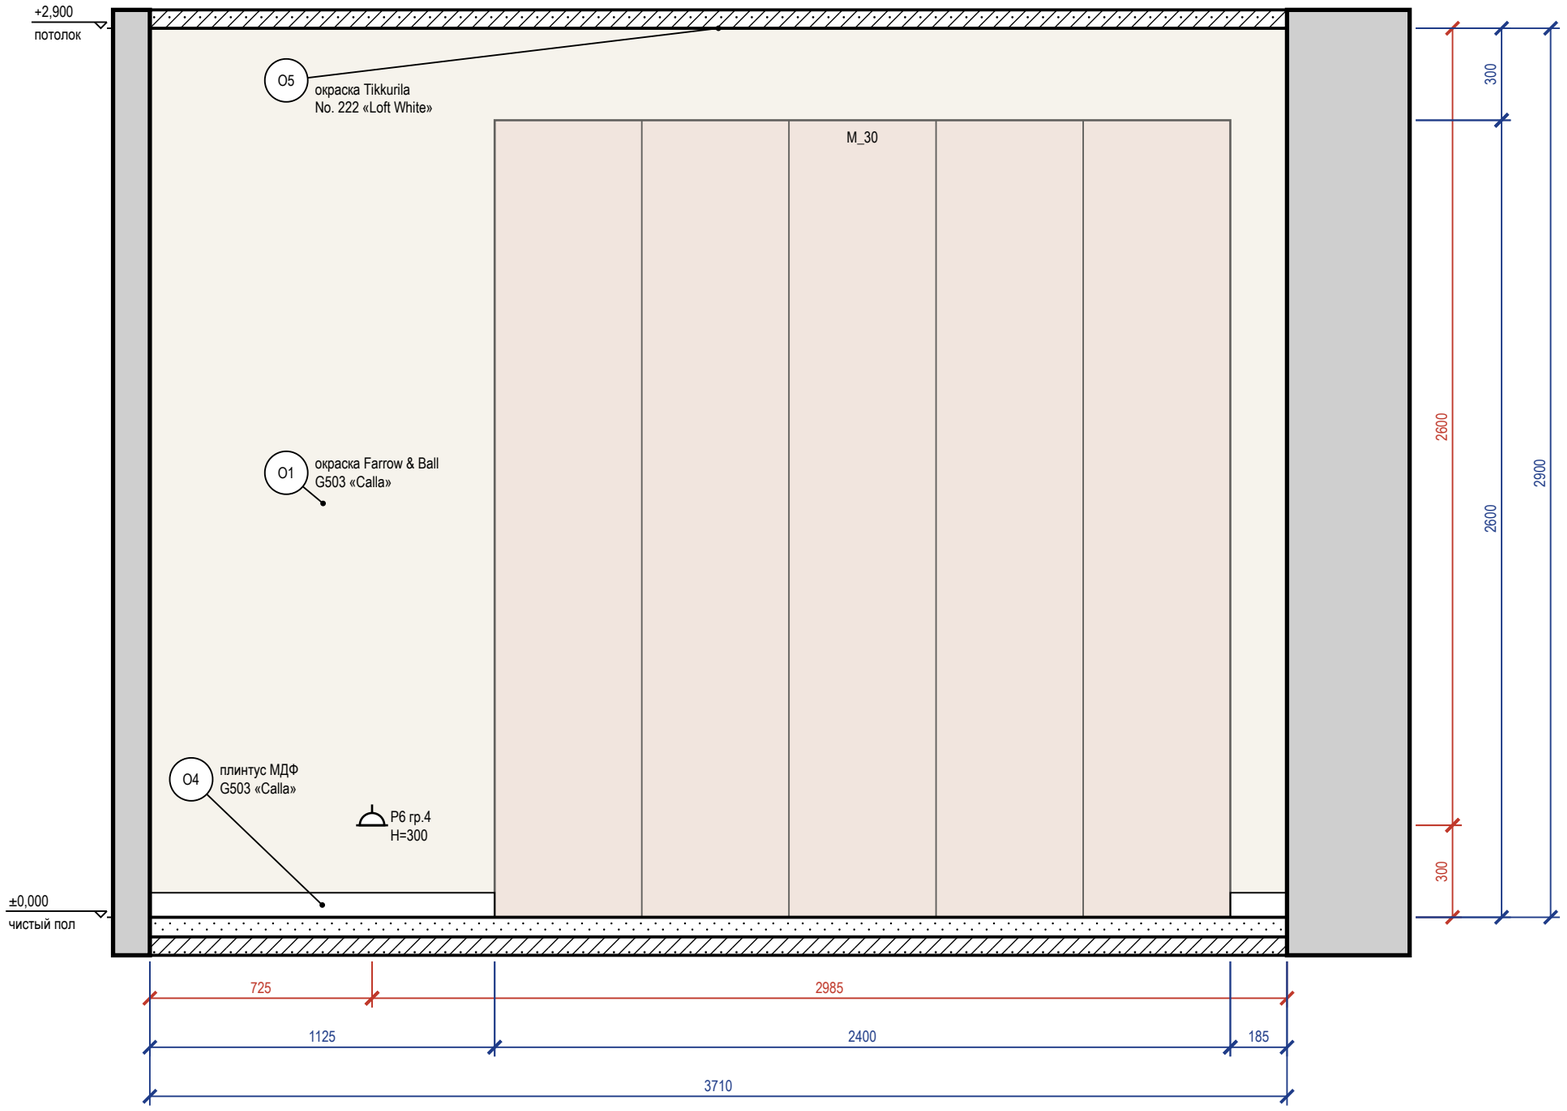



## Схема развёрток (М 1:100)

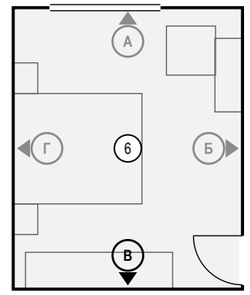


## Ведомость отделки (на листе)

| Марка | Поверхность | Материал, изделие | Цвет, код | Кол. |
|---|---|---|---|---|
| О1 | стены | окраска, Farrow & Ball Modern Emulsion, матовая, подготовка Q3 | Tikkurila G503 «Calla» | 10,8 м² |
| О4 | плинтус | плинтус МДФ, h 80 мм, аналог: плинтус МДФ под покраску 80×16 | Tikkurila G503 «Calla» | 1,3 м |
| О5 | потолок | окраска, Tikkurila Anti-Reflex 2, глубокоматовая, подготовка Q3 | Little Greene No. 222 «Loft White» | 17,2 м² |

**5** **Плинтус МДФ 80×16 мм у окрашенной стены (М 1:20)**
Узел 5 — лист С3

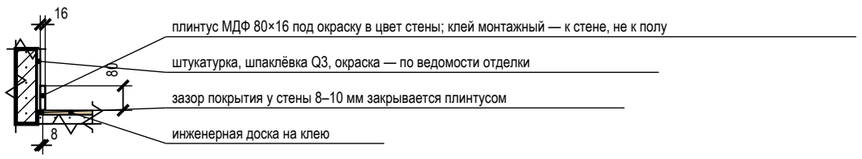


## Примечания


1. Размеры — в мм от чистовых поверхностей стен; условные обозначения и общие указания — лист 2.

| | | | | | |
|---|---|---|---|---|---|
| | | | | | Проект: Дом 120 м² |
| | Лист | № док. | Подпись | Дата | Развёртка стены В. Спальня родителей (пом. 6) |
| Дизайнер | Кырлан А.С. | | | 19.10.26 | |


| Стадия | Лист | Листов |
|---|---|---|
| П | 70 | 104 |

выпуск 19.10.2026 № 46d0102a0d · стр. 70 из 104

## Развёртка стены Г

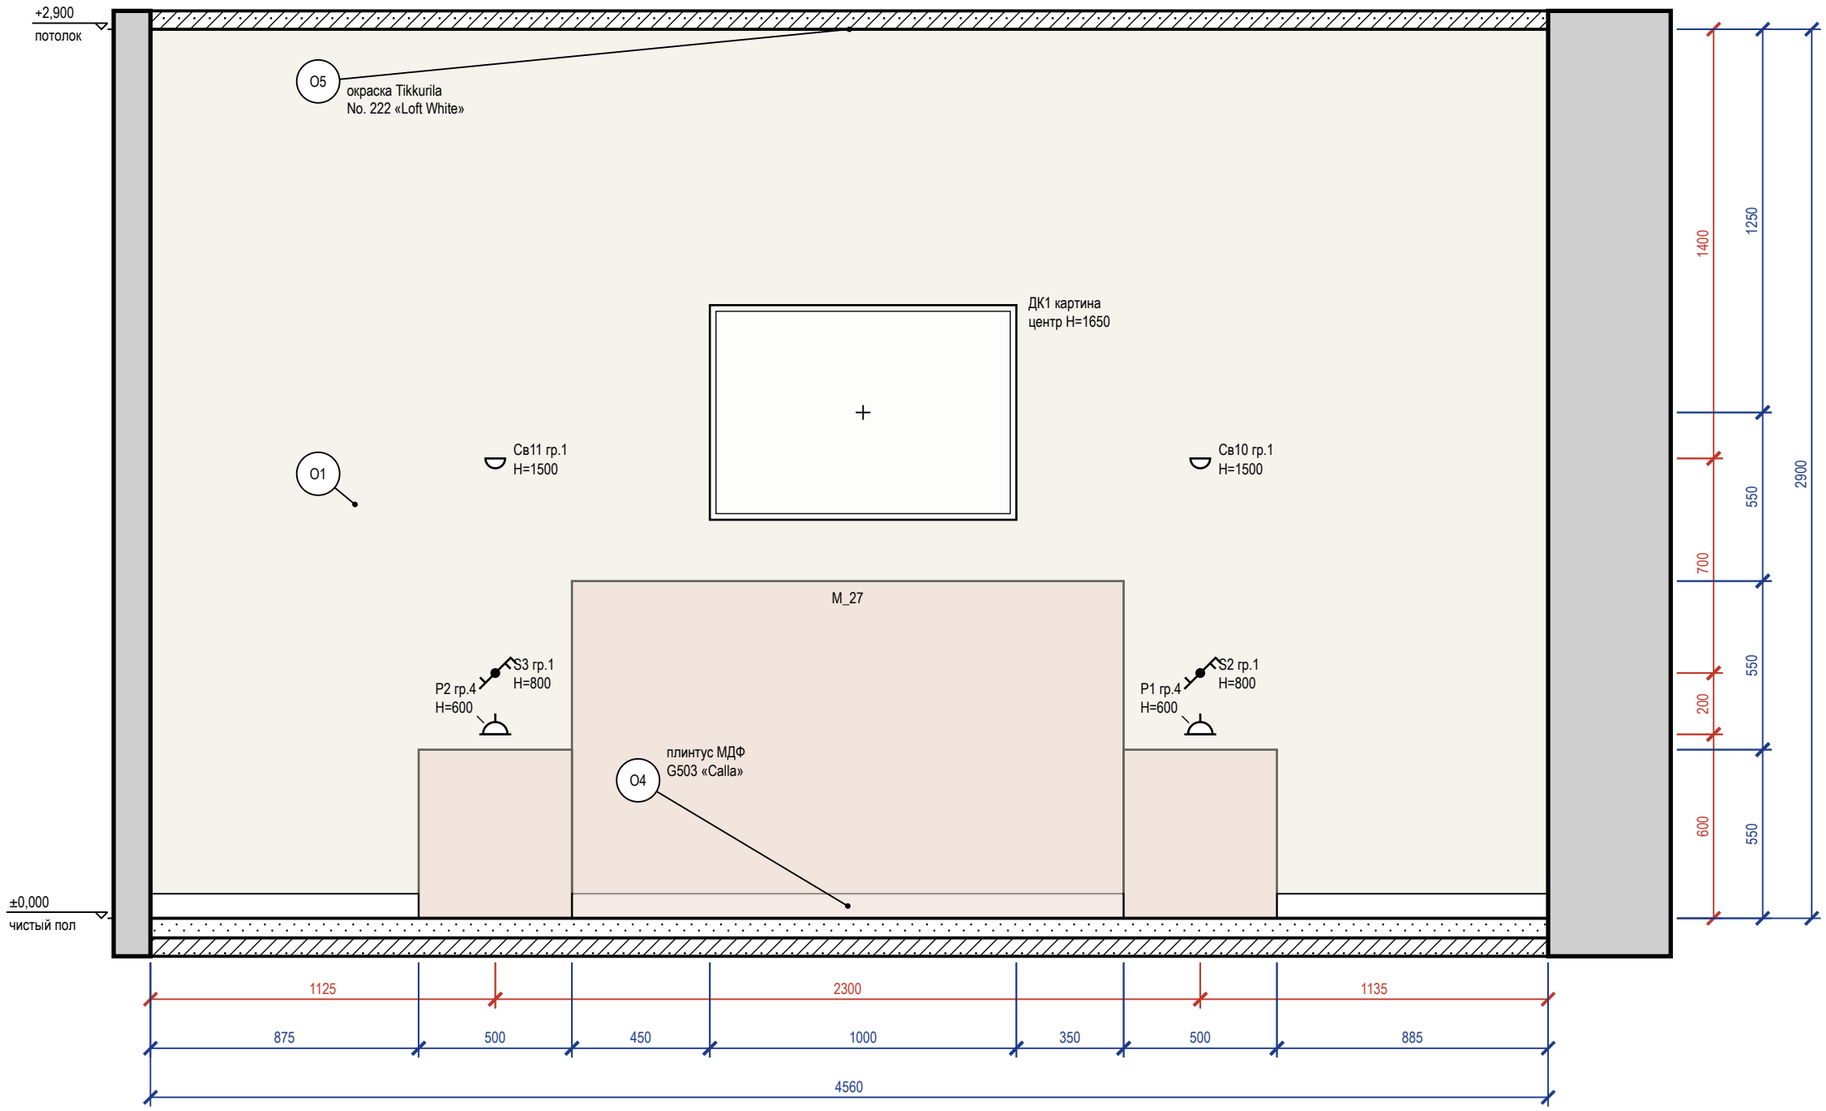


### Схема развёрток (М 1:100)

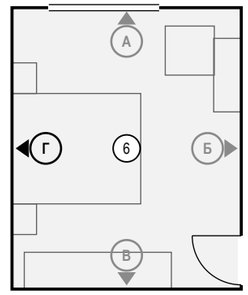


### Ведомость отделки (на листе)

| Марка | Поверхность | Материал, изделие | Цвет, код | Кол. |
|---|---|---|---|---|
| О1 | стены | окраска, Farrow & Ball Modern Emulsion, матовая, подготовка Q3 | Tikkurila G503 «Calla» | 13,2 м² |
| О4 | плинтус | плинтус МДФ, h 80 мм, аналог: плинтус МДФ под покраску 80×16 | Tikkurila G503 «Calla» | 3,6 м |
| О5 | потолок | окраска, Tikkurila Anti-Reflex 2, глубокоматовая, подготовка Q3 | Little Greene No. 222 «Loft White» | 17,2 м² |

### Примечания


1. Размеры — в мм от чистовых поверхностей стен; условные обозначения и общие указания — лист 2.
2. Картины и зеркала крепить к основанию по паспорту изделия (закладные и анкеры — в перечне скрытых работ); крест — ось центра предмета.

| | | | | | |
|---|---|---|---|---|---|
| | | | | | Проект: Дом 120 м² |
| | Лист | № док. | Подпись | Дата | Развёртка стены Г. Спальня родителей (пом. 6) |
| Дизайнер | Кырлан А.С. | | | 19.10.26 | |


| Стадия | Лист | Листов |
|---|---|---|
| П | 71 | 104 |

выпуск 19.10.2026 № 46d0102a0d · стр. 71 из 104

## Развёртка стены А

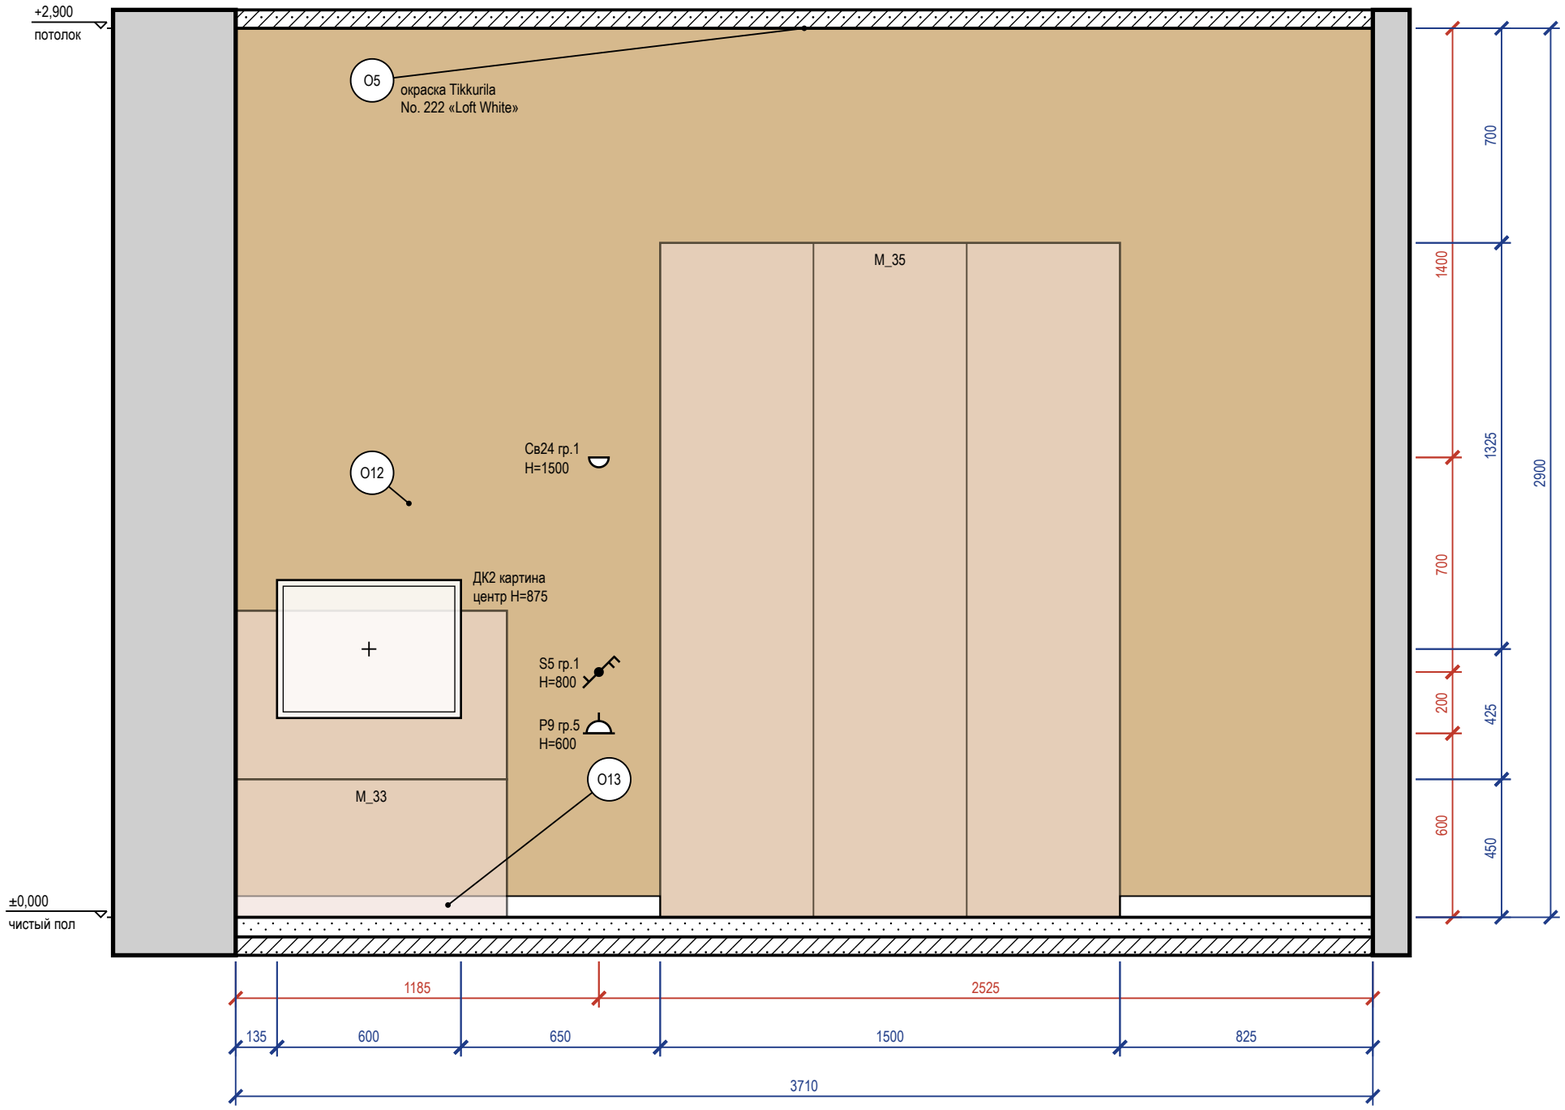


## Схема развёрток (М 1:100)

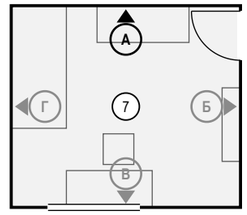


## Ведомость отделки (на листе)

| Марка | Поверхность | Материал, изделие | Цвет, код | Кол. |
|---|---|---|---|---|
| О5 | потолок | окраска, Tikkurila Anti-Reflex 2, глубокоматовая, подготовка Q3 | Little Greene No. 222 «Loft White» | 12,3 м² |
| О12 | акцентная стена | окраска, Farrow & Ball Modern Emulsion, матовая, подготовка Q3 | Farrow & Ball No. 66 «India Yellow — охра / горчица итальянских фасадов» | 10,8 м² |
| О13 | плинтус | плинтус МДФ, Orac Decor Contour (Luxxus), h 69 мм, SX165 | Tikkurila G503 «Calla» | 2,2 м |

### Примечания


1. Размеры — в мм от чистовых поверхностей стен; условные обозначения и общие указания — лист 2.
2. Картины и зеркала крепить к основанию по паспорту изделия (закладные и анкеры — в перечне скрытых работ); крест — ось центра предмета.

| | | | | | |
|---|---|---|---|---|---|
| | | | | | Проект: Дом 120 м² |
| | Лист | № док. | Подпись | Дата | |
| Дизайнер | Кырлан А.С. | | | 19.10.26 | Развёртка стены А. Детская (пом. 7) |


| Стадия | Лист | Листов |
|---|---|---|
| П | 72 | 104 |

выпуск 19.10.2026 № 46d0102a0d · стр. 72 из 104

## Развёртка стены Б

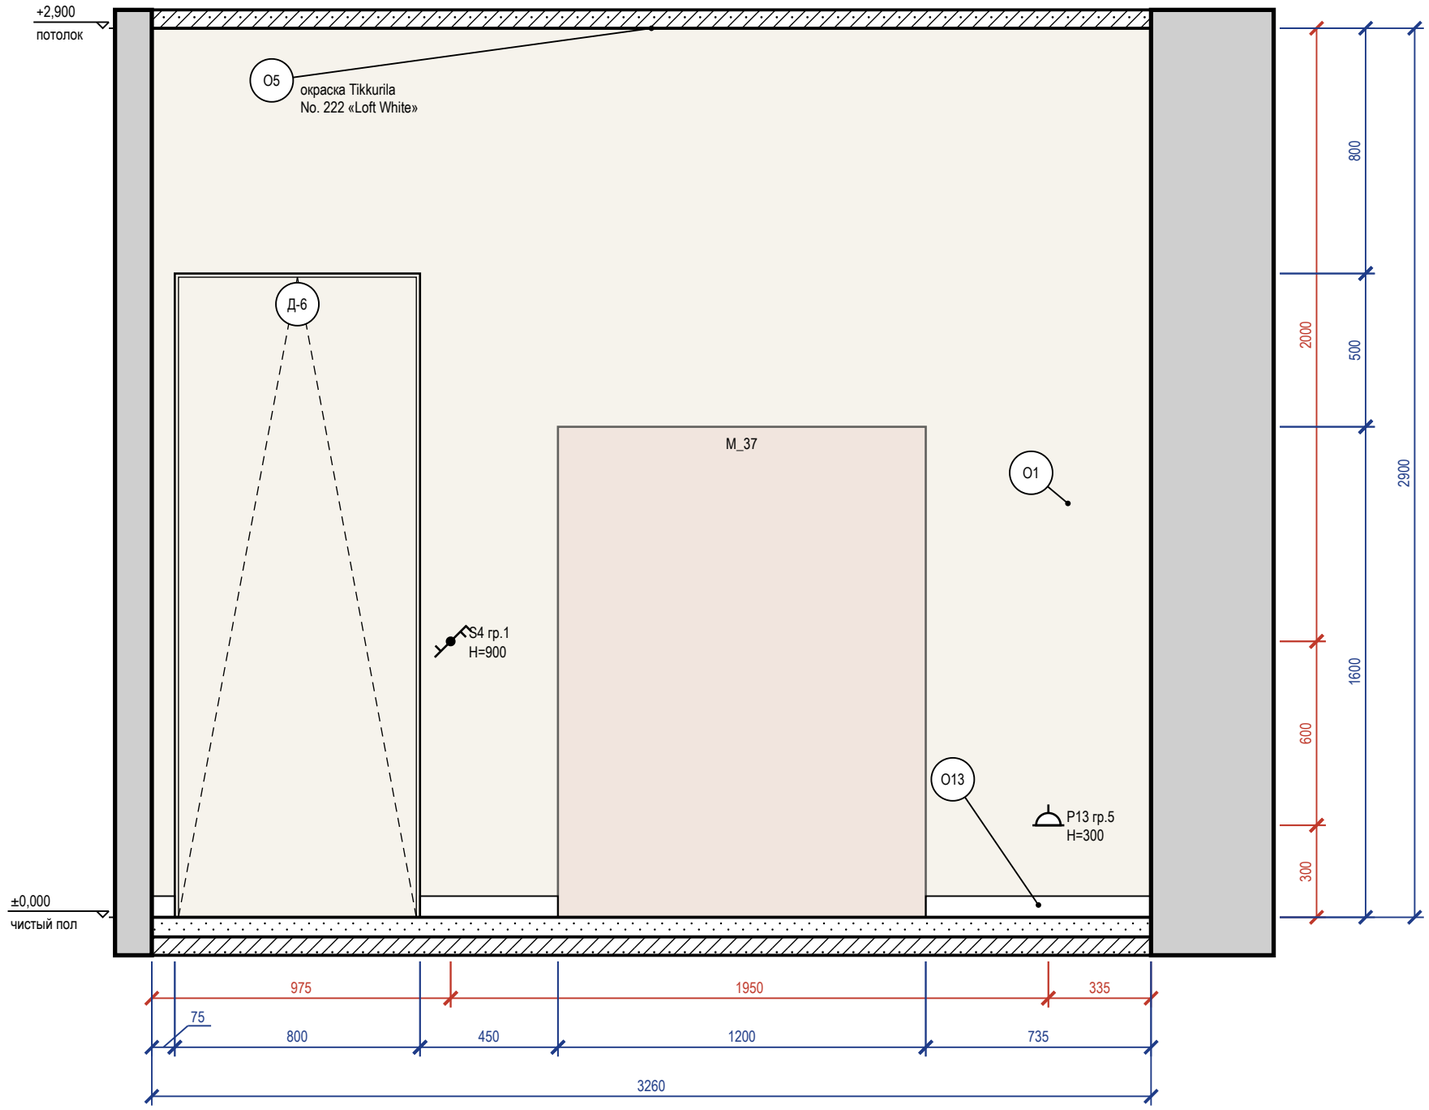


## Схема развёрток (М 1:100)

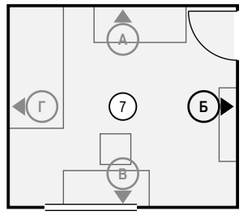


## Ведомость отделки (на листе)

| Марка | Поверхность | Материал, изделие | Цвет, код | Кол. |
|---|---|---|---|---|
| О1 | стены | окраска, Farrow & Ball Modern Emulsion, матовая, подготовка Q3 | Tikkurila G503 «Calla» | 7,8 м² |
| О5 | потолок | окраска, Tikkurila Anti-Reflex 2, глубокоматовая, подготовка Q3 | Little Greene No. 222 «Loft White» | 12,3 м² |
| О13 | плинтус | плинтус МДФ, Orac Decor Contour (Luxxus), h 69 мм, SX165 | Tikkurila G503 «Calla» | 1,3 м |

### Примечания


1. Размеры — в мм от чистовых поверхностей стен; условные обозначения и общие указания — лист 2.
2. Двери скрытого монтажа — полотно в плоскости стены, отделка стены по полотну, плинтус прерывается у короба (узел — на листе узлов).

| | | | | | |
|---|---|---|---|---|---|
| | | | | | Проект: Дом 120 м² |
| | Лист | № док. | Подпись | Дата | Развёртка стены Б. Детская (пом. 7) |
| Дизайнер | Кырлан А.С. | | | 19.10.26 | |


| Стадия | Лист | Листов |
|---|---|---|
| П | 73 | 104 |

выпуск 19.10.2026 № 46d0102a0d · стр. 73 из 104

## Развёртка стены В

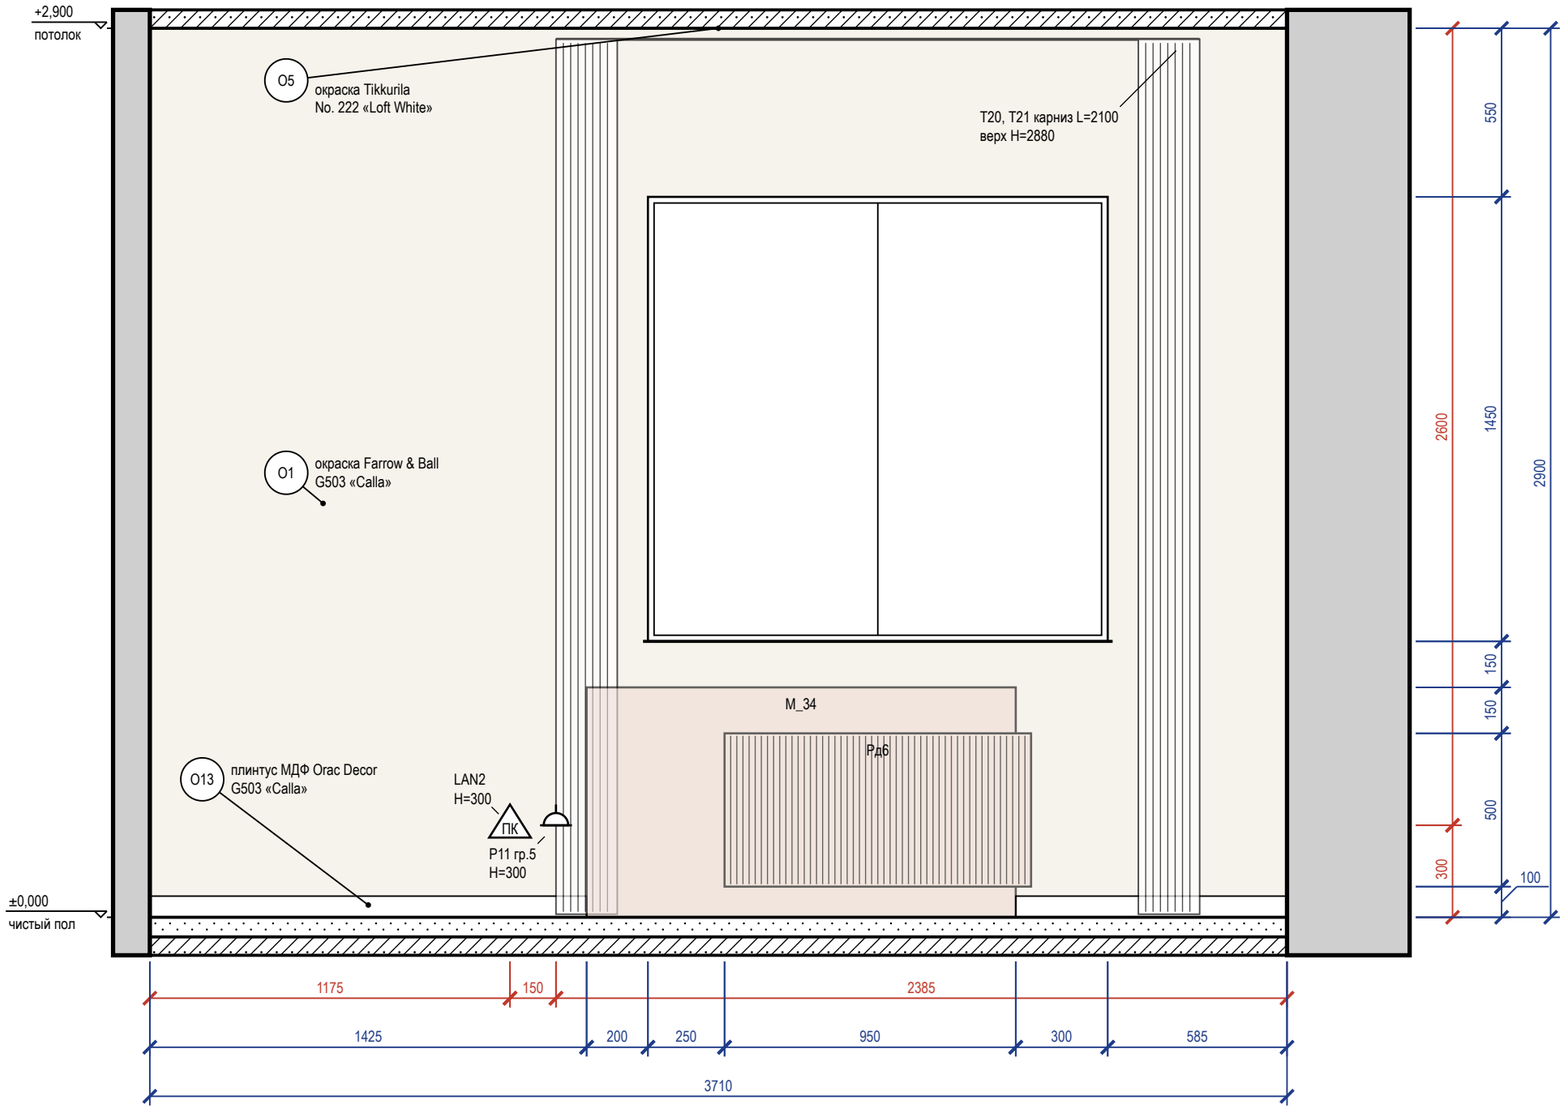


### Схема развёрток (М 1:100)

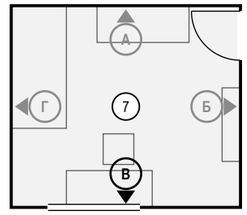


### Ведомость отделки (на листе)

| Марка | Поверхность | Материал, изделие | Цвет, код | Кол. |
|---|---|---|---|---|
| О1 | стены | окраска, Farrow & Ball Modern Emulsion, матовая, подготовка Q3 | Tikkurila G503 «Calla» | 8,6 м² |
| О5 | потолок | окраска, Tikkurila Anti-Reflex 2, глубокоматовая, подготовка Q3 | Little Greene No. 222 «Loft White» | 12,3 м² |
| О13 | плинтус | плинтус МДФ, Orac Decor Contour (Luxxus), h 69 мм, SX165 | Tikkurila G503 «Calla» | 2,3 м |

### Примечания

1. Размеры — в мм от чистовых поверхностей стен; условные обозначения и общие указания — лист 2.
2. Карнизы (шины) — по ведомости текстиля декоратора; длина L и верх H — по развёртке, крепление — до окраски потолка.


| | | | | | |
|---|---|---|---|---|---|
| | Лист | № док. | Подпись | Дата | |
| Дизайнер | Кырлан А.С. | | | 19.10.26 | Развёртка стены В. Детская (пом. 7) |

Проект: Дом 120 м²


| Стадия | Лист | Листов |
|---|---|---|
| П | 74 | 104 |

выпуск 19.10.2026 № 46d0102a0d · стр. 74 из 104

## Развёртка стены Г

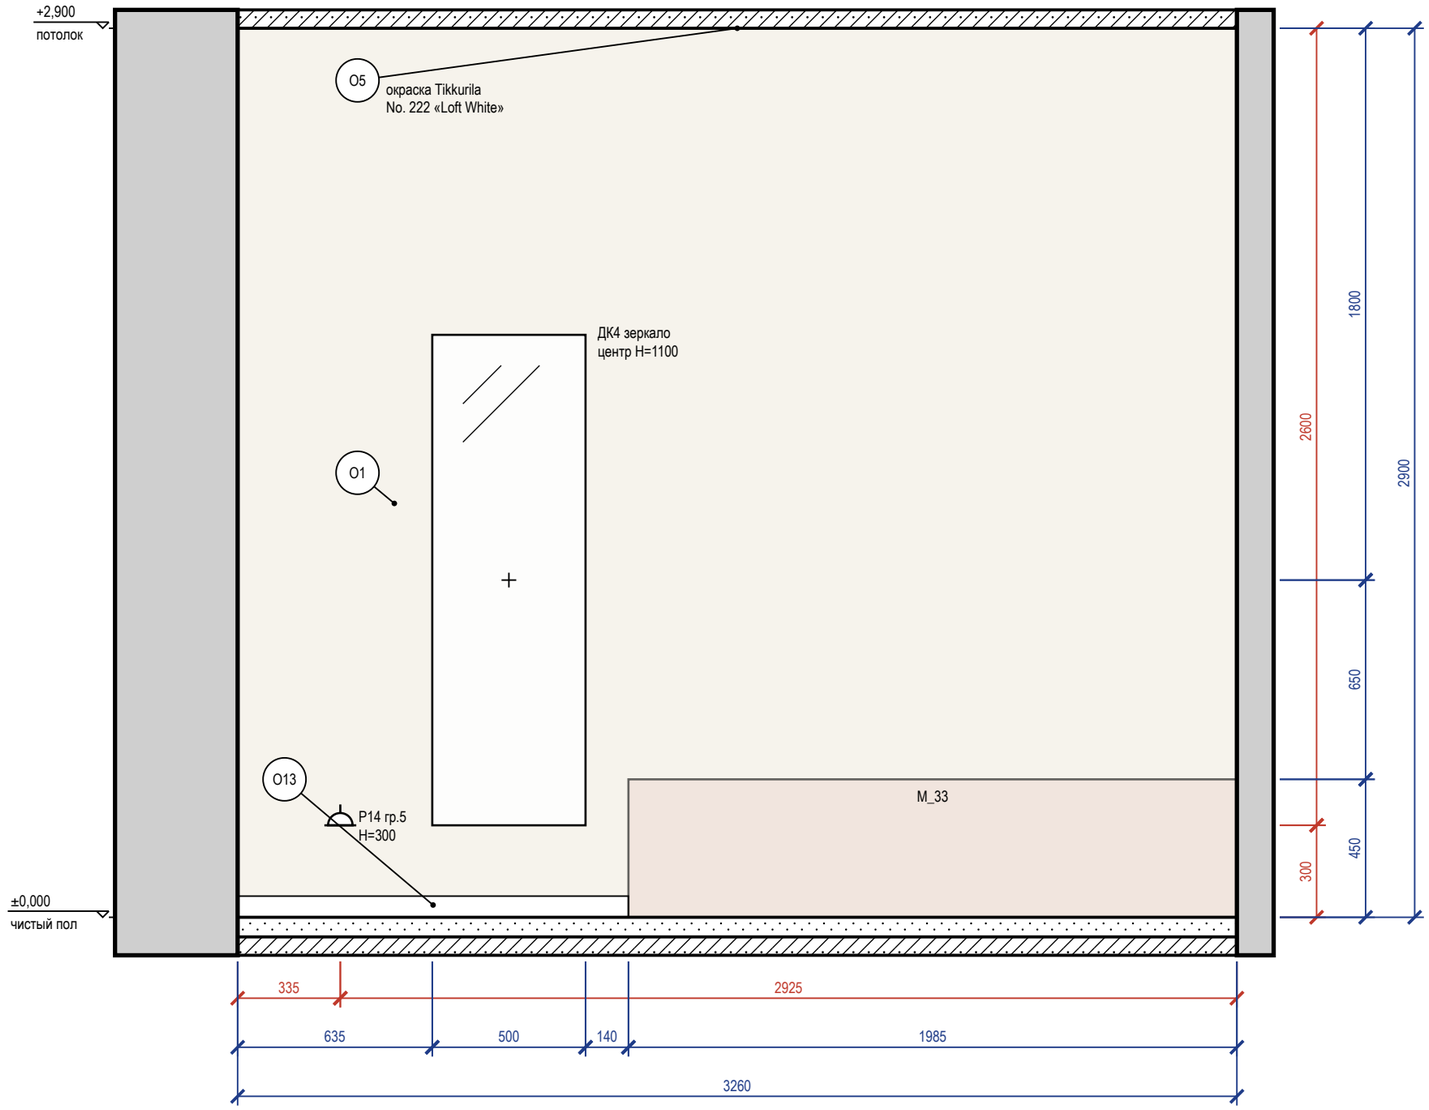


## Схема развёрток (М 1:100)

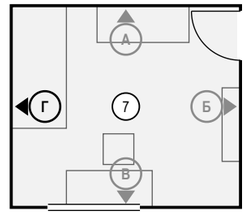


## Ведомость отделки (на листе)

| Марка | Поверхность | Материал, изделие | Цвет, код | Кол. |
|---|---|---|---|---|
| О1 | стены | окраска, Farrow & Ball Modern Emulsion, матовая, подготовка Q3 | Tikkurila G503 «Calla» | 9,5 м² |
| О5 | потолок | окраска, Tikkurila Anti-Reflex 2, глубокоматовая, подготовка Q3 | Little Greene No. 222 «Loft White» | 12,3 м² |
| О13 | плинтус | плинтус МДФ, Orac Decor Contour (Luxxus), h 69 мм, SX165 | Tikkurila G503 «Calla» | 1,3 м |

### Примечания


1. Размеры — в мм от чистовых поверхностей стен; условные обозначения и общие указания — лист 2.
2. Картины и зеркала крепить к основанию по паспорту изделия (закладные и анкеры — в перечне скрытых работ); крест — ось центра предмета.

| | | | | | |
|---|---|---|---|---|---|
| | | | | | Проект: Дом 120 м² |
| | Лист | № док. | Подпись | Дата | |
| Дизайнер | Кырлан А.С. | | | 19.10.26 | Развёртка стены Г. Детская (пом. 7) |


| Стадия | Лист | Листов |
|---|---|---|
| П | 75 | 104 |

выпуск 19.10.2026 № 46d0102a0d · стр. 75 из 104


## Развёртка стены А

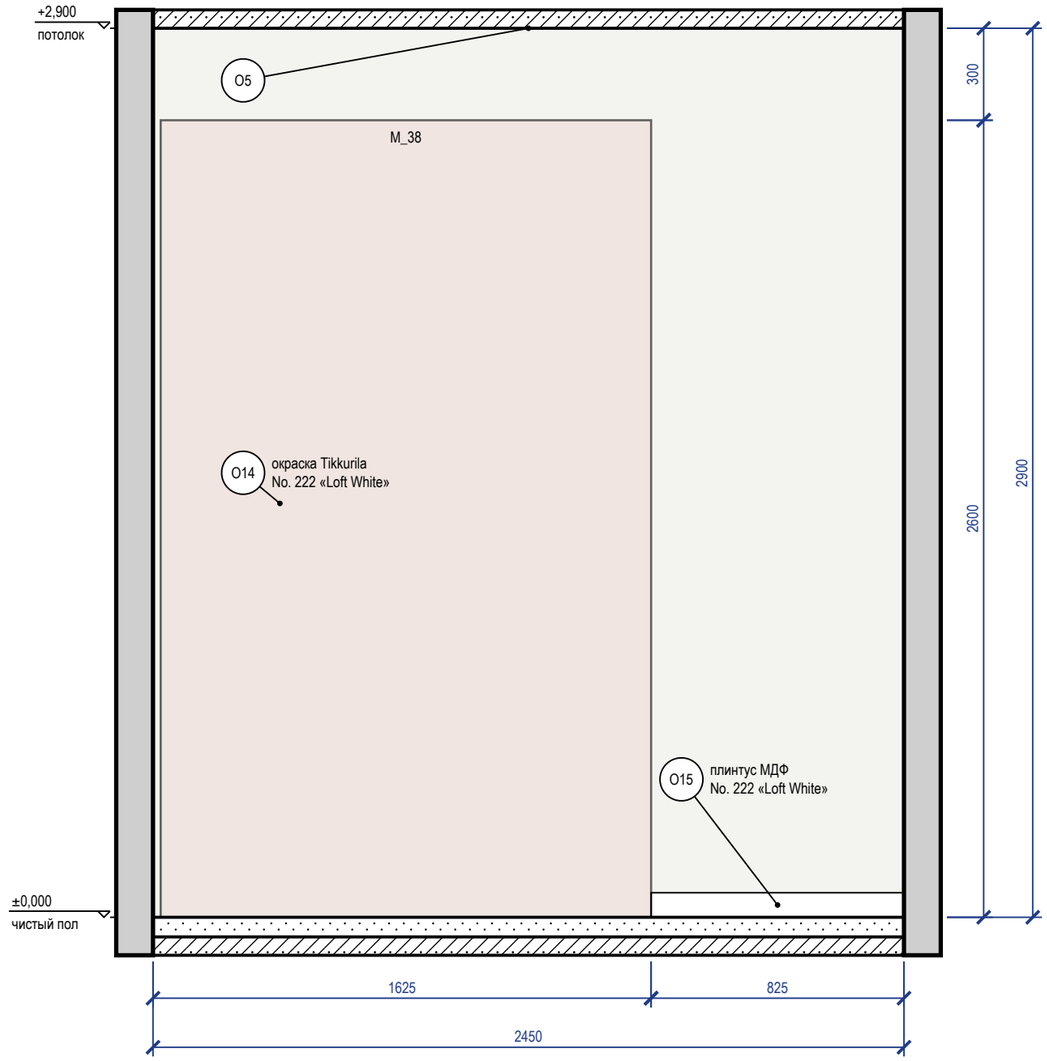


## Развёртка стены Б

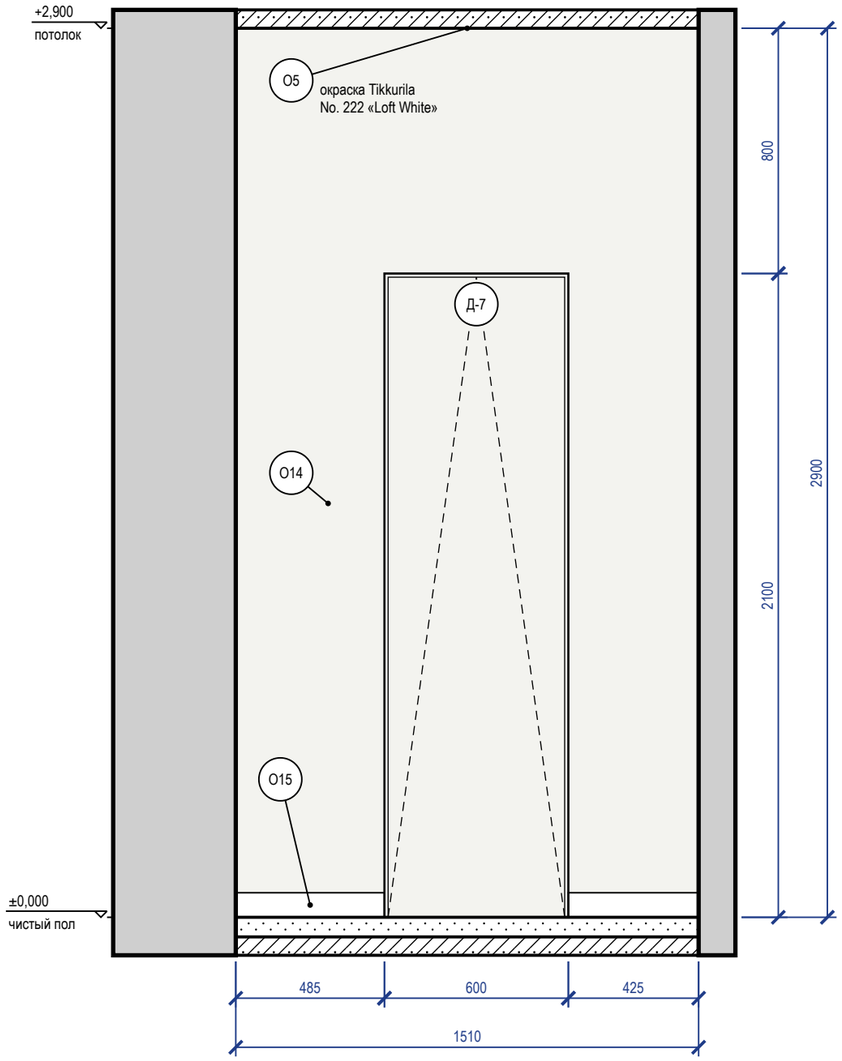


### Схема развёрток (М 1:100)

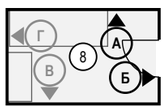


### Ведомость отделки (на листе)

| Марка | Поверхность | Материал, изделие | Цвет, код | Кол. |
|---|---|---|---|---|
| О5 | потолок | окраска, Tikkurila Anti-Reflex 2, глубокоматовая, подготовка Q3 | Little Greene No. 222 «Loft White» | 3,8 м² |
| О14 | стены | окраска, Tikkurila Harmony, матовая, подготовка Q3 | Little Greene No. 222 «Loft White» | 10,2 м² |
| О15 | плинтус | плинтус МДФ, h 80 мм, аналог: плинтус МДФ под покраску 80×16 | Little Greene No. 222 «Loft White» | 1,7 м |

### Примечания


1. Размеры — в мм от чистовых поверхностей стен; условные обозначения и общие указания — лист 2.
2. Двери скрытого монтажа — полотно в плоскости стены, отделка стены по полотну, плинтус прерывается у короба (узел — на листе узлов).

| | | | | | |
|---|---|---|---|---|---|
| | | | | | Проект: Дом 120 м² |
| | Лист | № док. | Подпись | Дата | Развёртки стен А, Б. Гардеробная (пом. 8) |
| Дизайнер | Кырлан А.С. | | | 19.10.26 | |


| Стадия | Лист | Листов |
|---|---|---|
| П | 76 | 104 |

выпуск 19.10.2026 № 46d0102a0d · стр. 76 из 104


## Развёртка стены В

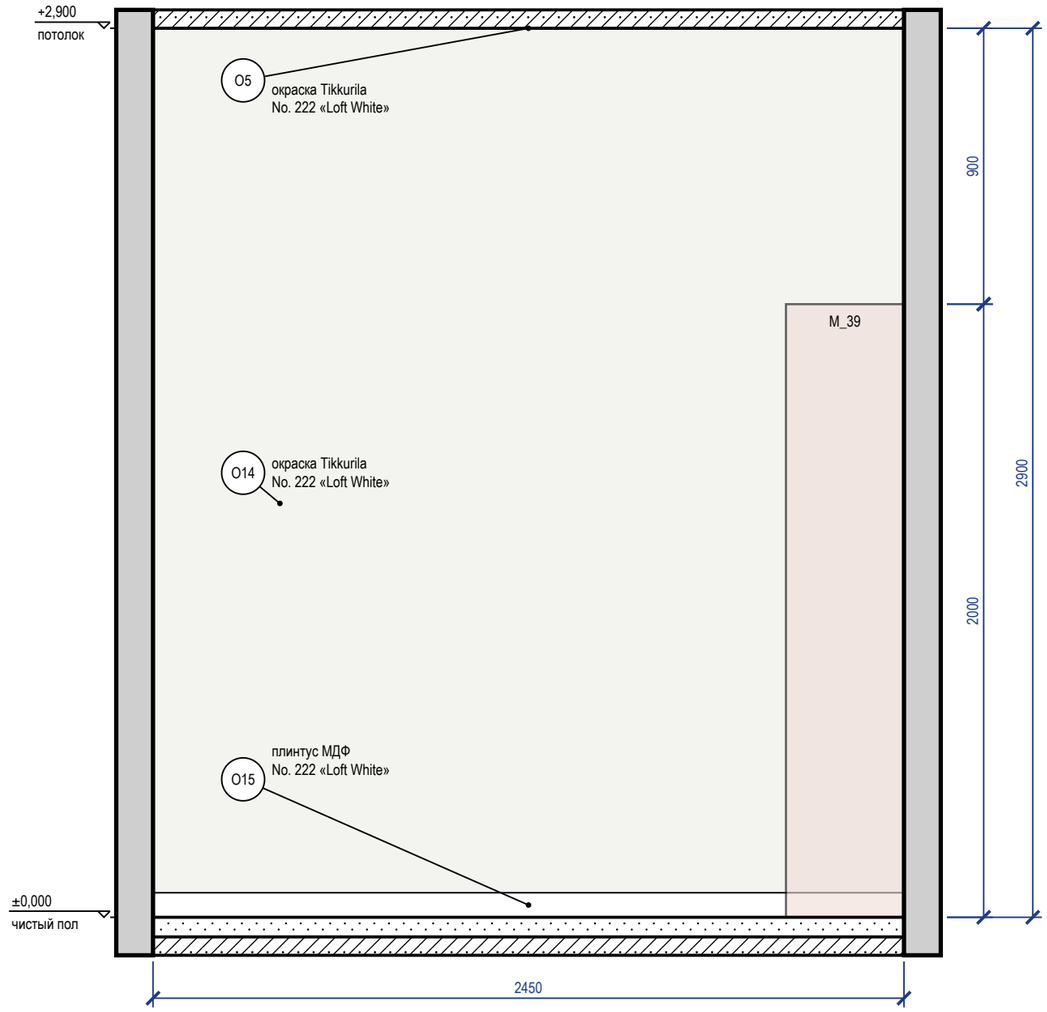


## Развёртка стены Г

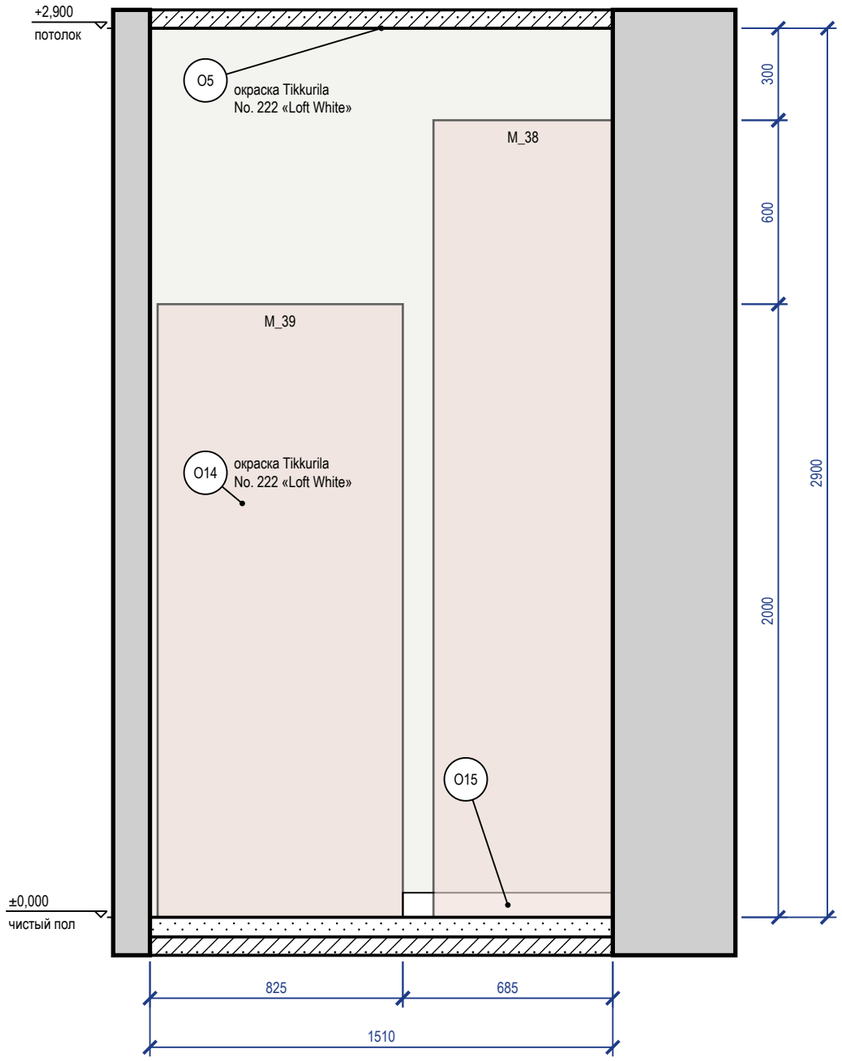


### Схема развёрток (М 1:100)

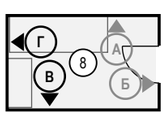


### Ведомость отделки (на листе)

| Марка | Поверхность | Материал, изделие | Цвет, код | Кол. |
|---|---|---|---|---|
| О5 | потолок | окраска, Tikkurila Anti-Reflex 2, глубокоматовая, подготовка Q3 | Little Greene No. 222 «Loft White» | 3,8 м² |
| О14 | стены | окраска, Tikkurila Harmony, матовая, подготовка Q3 | Little Greene No. 222 «Loft White» | 11,5 м² |
| О15 | плинтус | плинтус МДФ, h 80 мм, аналог: плинтус МДФ под покраску 80×16 | Little Greene No. 222 «Loft White» | 3,1 м |

### Примечания


1. Размеры — в мм от чистовых поверхностей стен; условные обозначения и общие указания — лист 2.

| | | | | | |
|---|---|---|---|---|---|
| | | | | | Проект: Дом 120 м² |
| | Лист | № док. | Подпись | Дата | Развёртки стен В, Г. Гардеробная (пом. 8) |
| Дизайнер | Кырлан А.С. | | | 19.10.26 | |


| Стадия | Лист | Листов |
|---|---|---|
| П | 77 | 104 |

выпуск 19.10.2026 № 46d0102a0d · стр. 77 из 104


## Развёртка стены Б

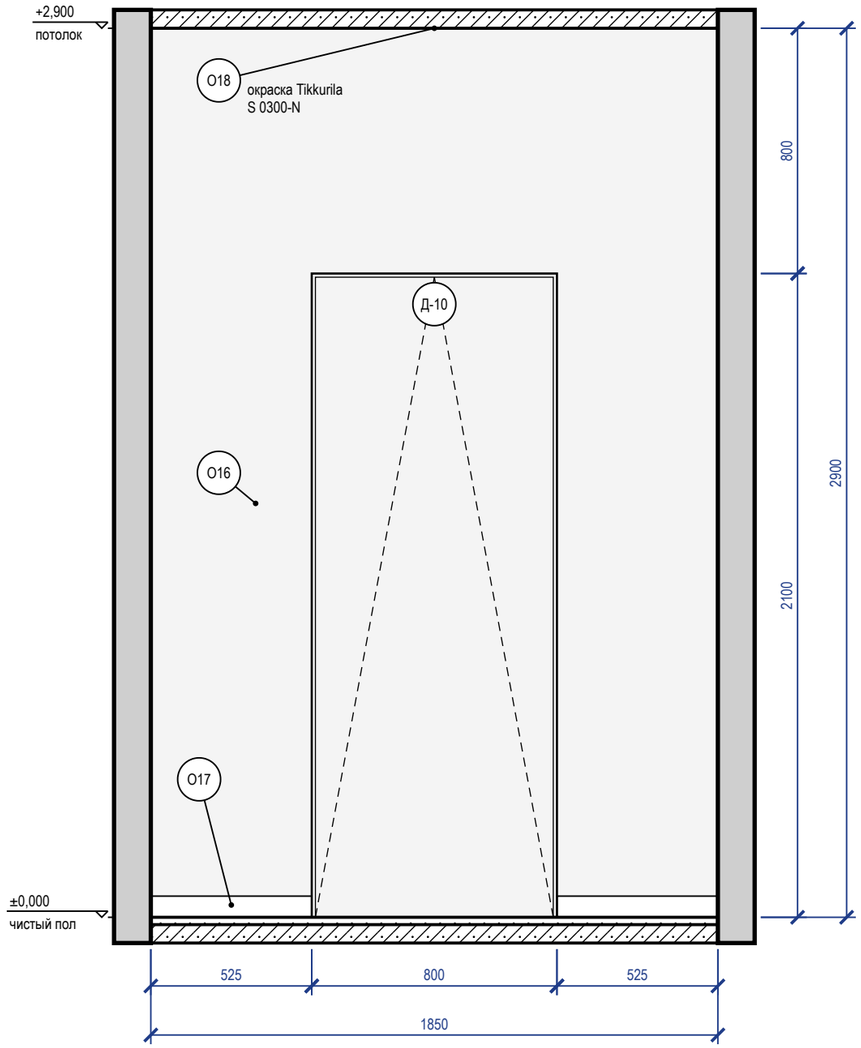


## Развёртка стены В

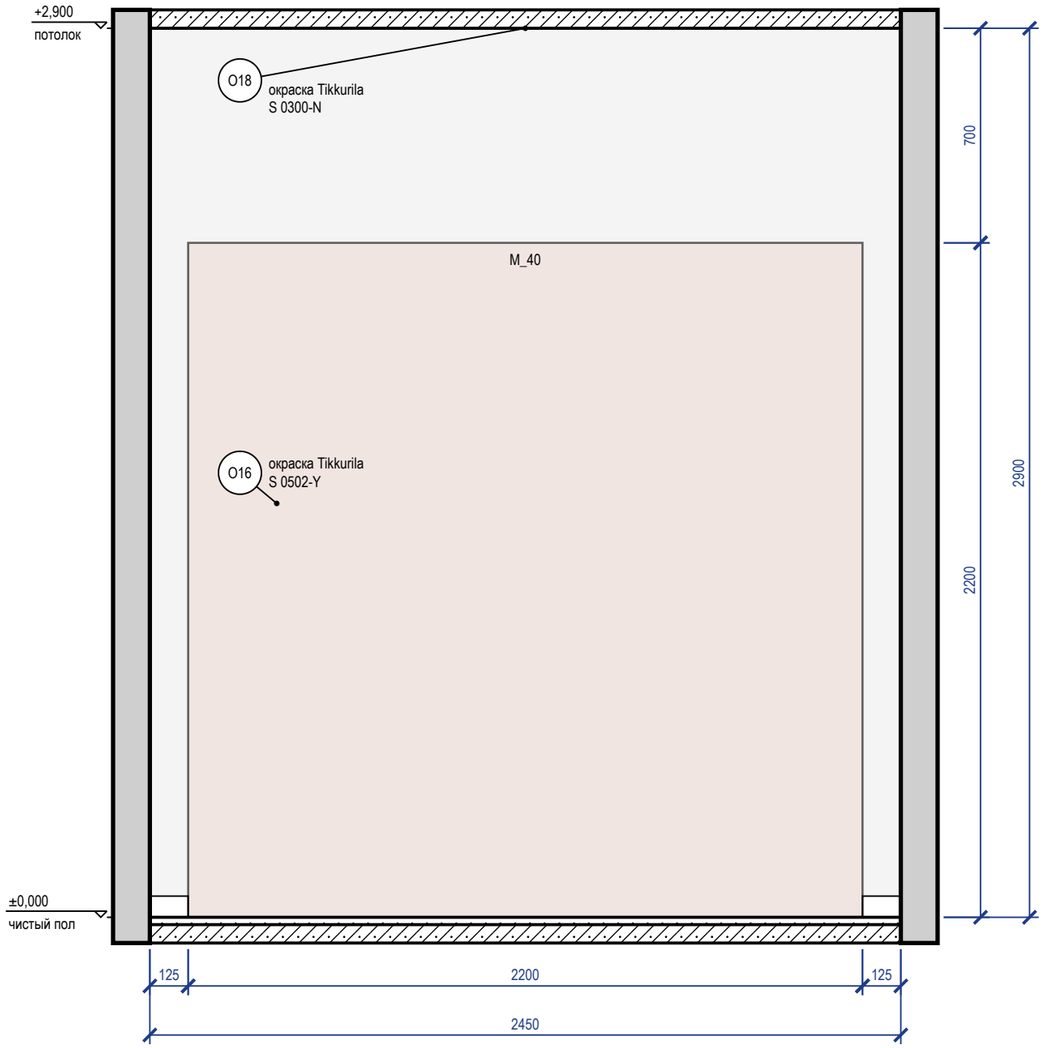


### Схема развёрток (М 1:100)

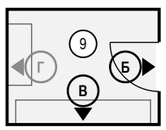


### Ведомость отделки (на листе)

| Марка | Поверхность | Материал, изделие | Цвет, код | Кол. |
|---|---|---|---|---|
| О16 | стены | окраска, Tikkurila, матовая, подготовка Q3 | NCS S 0502-Y | 10,8 м² |
| О17 | плинтус | плинтус МДФ, Orac Decor Contour (Luxxus), h 69 мм, SX165, шелковисто-матовая | NCS S 0300-N | 1,3 м |
| О18 | потолок | окраска, Tikkurila, глубокоматовая | NCS S 0300-N | 4,7 м² |

### Примечания


1. Размеры — в мм от чистовых поверхностей стен; условные обозначения и общие указания — лист 2.
2. Двери скрытого монтажа — полотно в плоскости стены, отделка стены по полотну, плинтус прерывается у короба (узел — на листе узлов).

| | | | | | |
|---|---|---|---|---|---|
| | | | | | Проект: Дом 120 м² |
| | Лист | № док. | Подпись | Дата | Развёртки стен Б, В. Кладовая (пом. 9) |
| Дизайнер | Кырлан А.С. | | | 19.10.26 | |


| Стадия | Лист | Листов |
|---|---|---|
| П | 78 | 104 |

выпуск 19.10.2026 № 46d0102a0d · стр. 78 из 104

## Развёртка стены Г

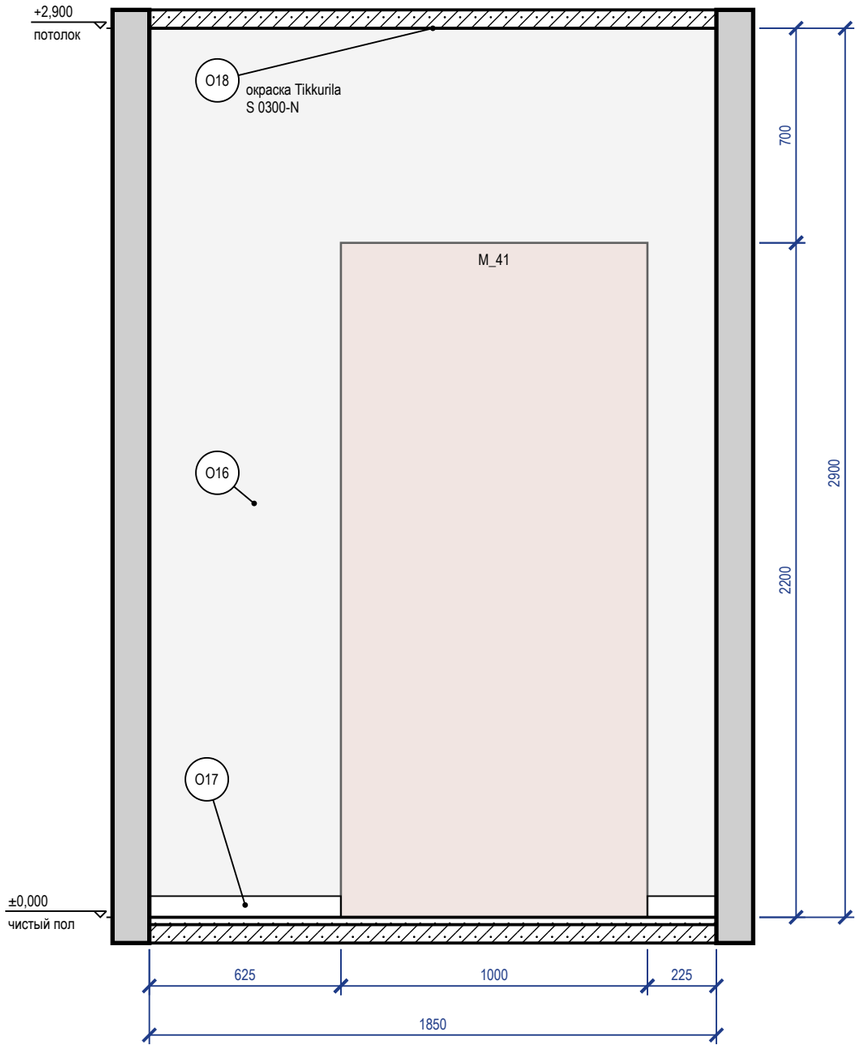


## Схема развёрток (М 1:100)

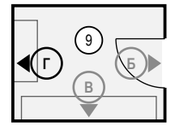


## Ведомость отделки (на листе)

| Марка | Поверхность | Материал, изделие | Цвет, код | Кол. |
|---|---|---|---|---|
| О16 | стены | окраска, Tikkurila, матовая, подготовка Q3 | NCS S 0502-Y | 5,4 м² |
| О17 | плинтус | плинтус МДФ, Orac Decor Contour (Luxxus), h 69 мм, SX165, шелковисто-матовая | NCS S 0300-N | 0,8 м |
| О18 | потолок | окраска, Tikkurila, глубокоматовая | NCS S 0300-N | 4,7 м² |


## Примечания

1. Размеры — в мм от чистовых поверхностей стен; условные обозначения и общие указания — лист 2.


| | | | | | | |
|---|---|---|---|---|---|---|
| | | | | | Проект: Дом 120 м² | |
| | Лист | № док. | Подпись | Дата | | |
| Дизайнер | Кырлан А.С. | | | 19.10.26 | Развёртка стены Г. Кладовая (пом. 9) | Стадия: П; Лист: 79; Листов: 104 |

выпуск 19.10.2026 № 46d0102a0d · стр. 79 из 104

## Развёртка стены А

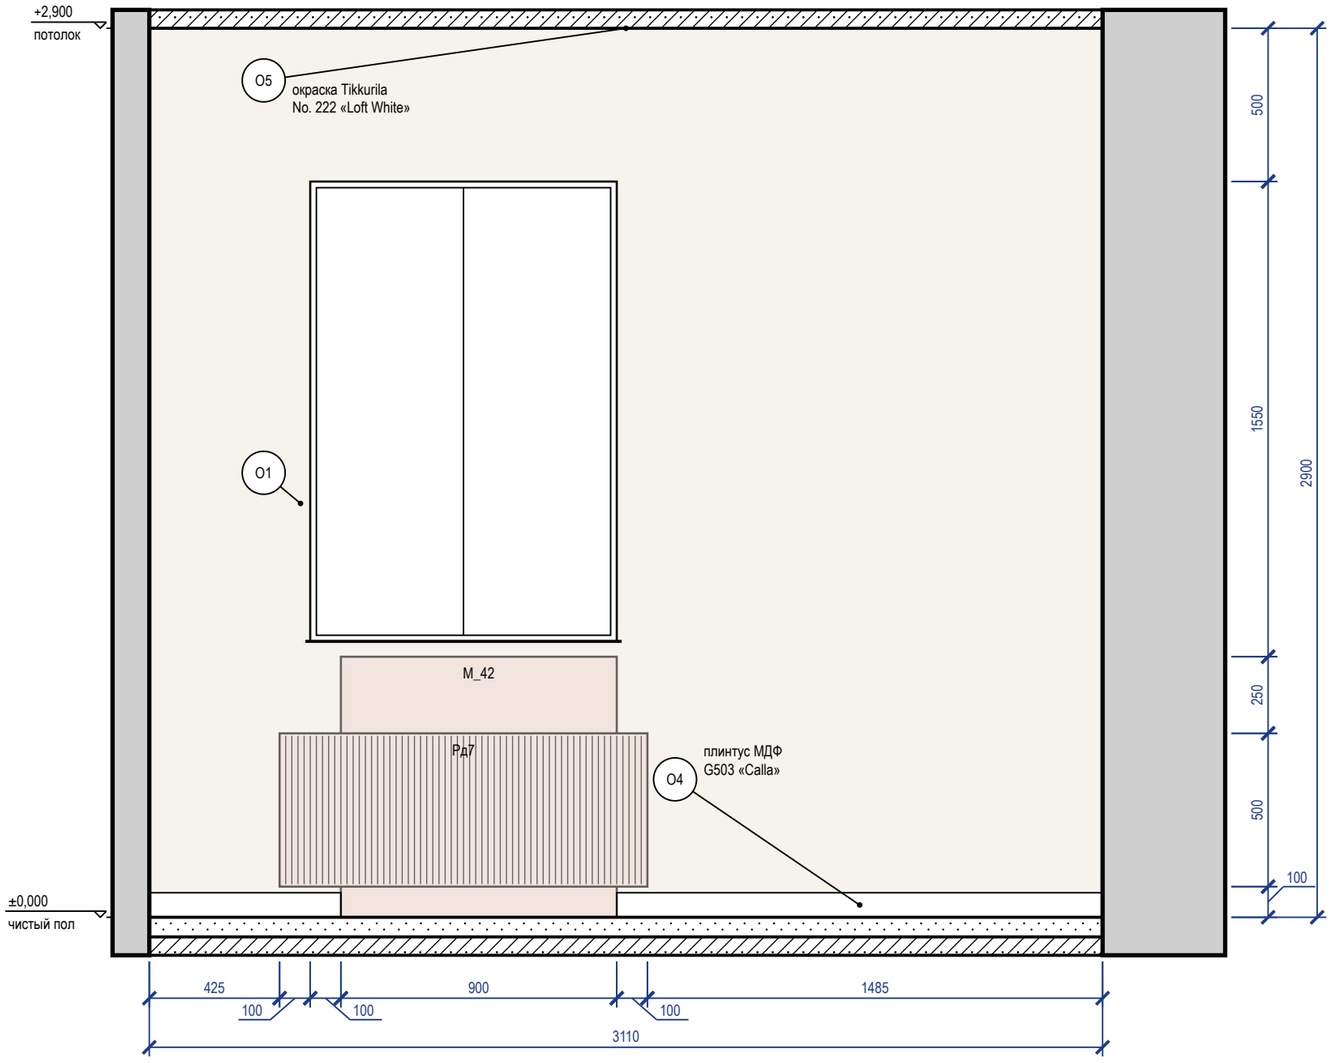


## Схема развёрток (М 1:100)

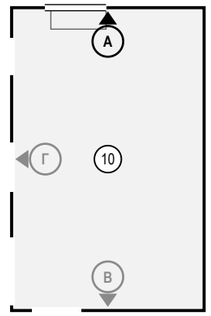


## Ведомость отделки (на листе)

| Марка | Поверхность | Материал, изделие | Цвет, код | Кол. |
|---|---|---|---|---|
| О1 | стены | окраска, Farrow & Ball Modern Emulsion, матовая, подготовка Q3 | Tikkurila G503 «Calla» | 7,5 м² |
| О4 | плинтус | плинтус МДФ, h 80 мм, аналог: плинтус МДФ под покраску 80×16 | Tikkurila G503 «Calla» | 2,2 м |
| О5 | потолок | окраска, Tikkurila Anti-Reflex 2, глубокоматовая, подготовка Q3 | Little Greene No. 222 «Loft White» | 15,5 м² |

## Примечания


1. Размеры — в мм от чистовых поверхностей стен; условные обозначения и общие указания — лист 2.

| | | | | | |
|---|---|---|---|---|---|
| | Лист | № док. | Подпись | Дата | Проект: Дом 120 м² |
| Дизайнер | Кырлан А.С. | | | 19.10.26 | Развёртка стены А. Холл второго этажа (пом. 10) |


| Стадия | Лист | Листов |
|---|---|---|
| П | 80 | 104 |

выпуск 19.10.2026 № 46d0102a0d · стр. 80 из 104

## Развёртка стены В

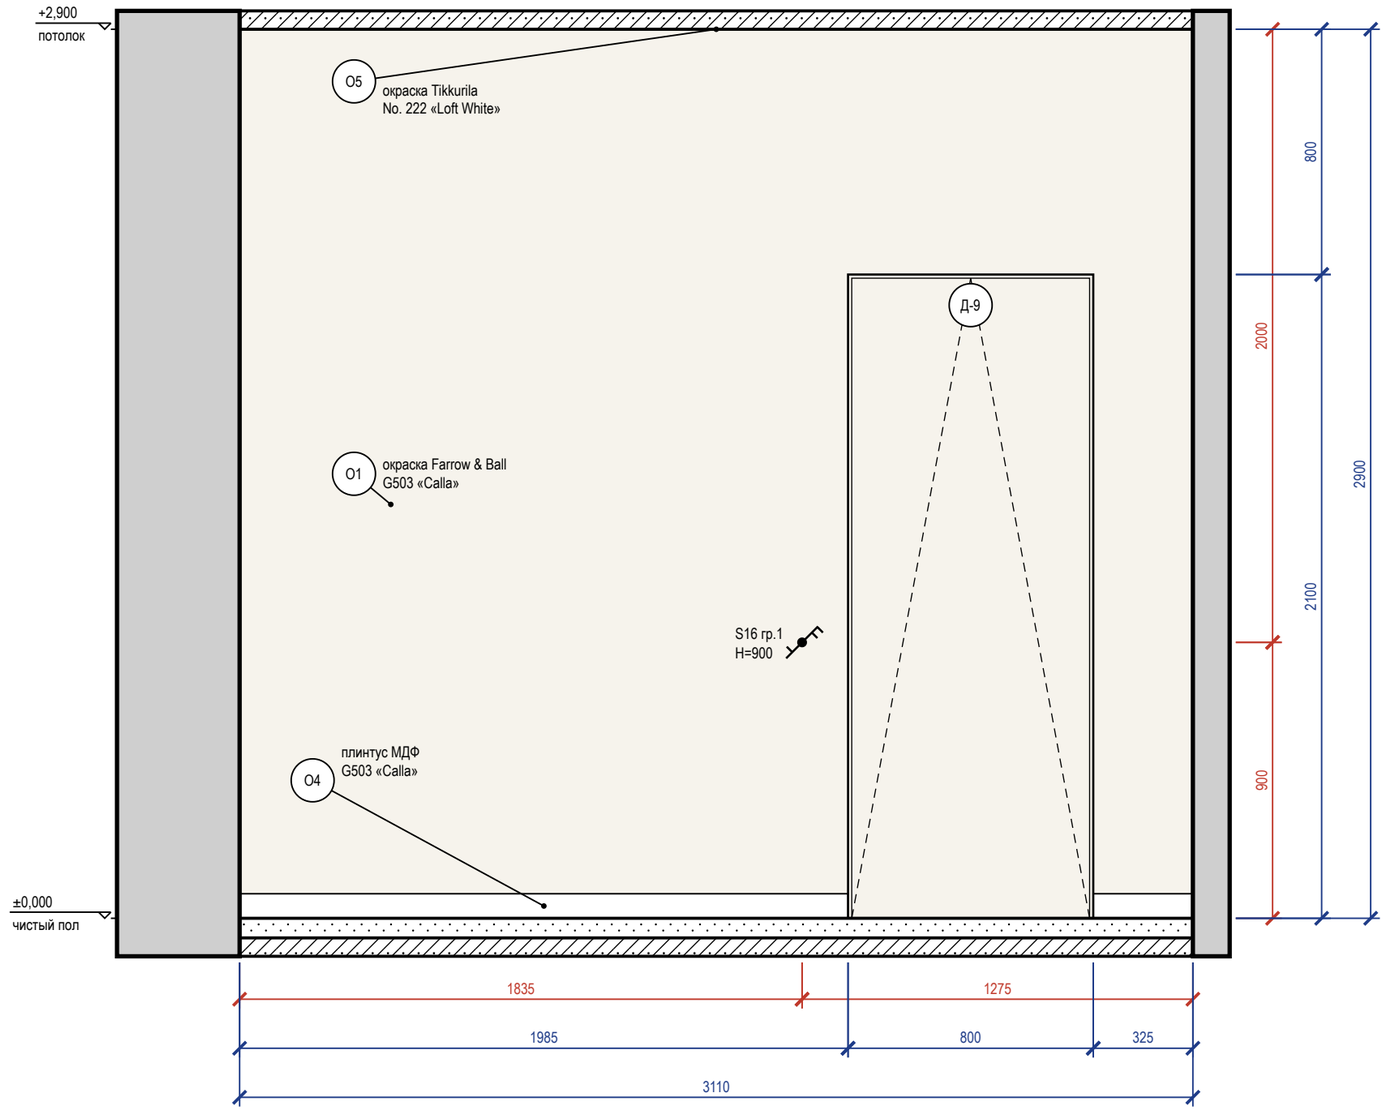


## Схема развёрток (М 1:100)

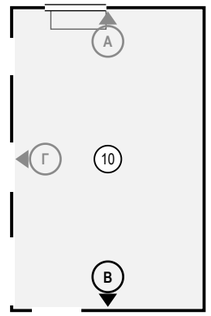


## Ведомость отделки (на листе)

| Марка | Поверхность | Материал, изделие | Цвет, код | Кол. |
|---|---|---|---|---|
| О1 | стены | окраска, Farrow & Ball Modern Emulsion, матовая, подготовка Q3 | Tikkurila G503 «Calla» | 7,3 м² |
| О4 | плинтус | плинтус МДФ, h 80 мм, аналог: плинтус МДФ под покраску 80×16 | Tikkurila G503 «Calla» | 2,3 м |
| О5 | потолок | окраска, Tikkurila Anti-Reflex 2, глубокоматовая, подготовка Q3 | Little Greene No. 222 «Loft White» | 15,5 м² |

## Примечания


1. Размеры — в мм от чистовых поверхностей стен; условные обозначения и общие указания — лист 2.
2. Двери скрытого монтажа — полотно в плоскости стены, отделка стены по полотну, плинтус прерывается у короба (узел — на листе узлов).

| | | | | | |
|---|---|---|---|---|---|
| | | | | | Проект: Дом 120 м² |
| | Лист | № док. | Подпись | Дата | Развёртка стены В. Холл второго этажа (пом. 10) |
| Дизайнер | Кырлан А.С. | | | 19.10.26 | |


| Стадия | Лист | Листов |
|---|---|---|
| П | 81 | 104 |

выпуск 19.10.2026 № 46d0102a0d · стр. 81 из 104

## Развёртка стены Г

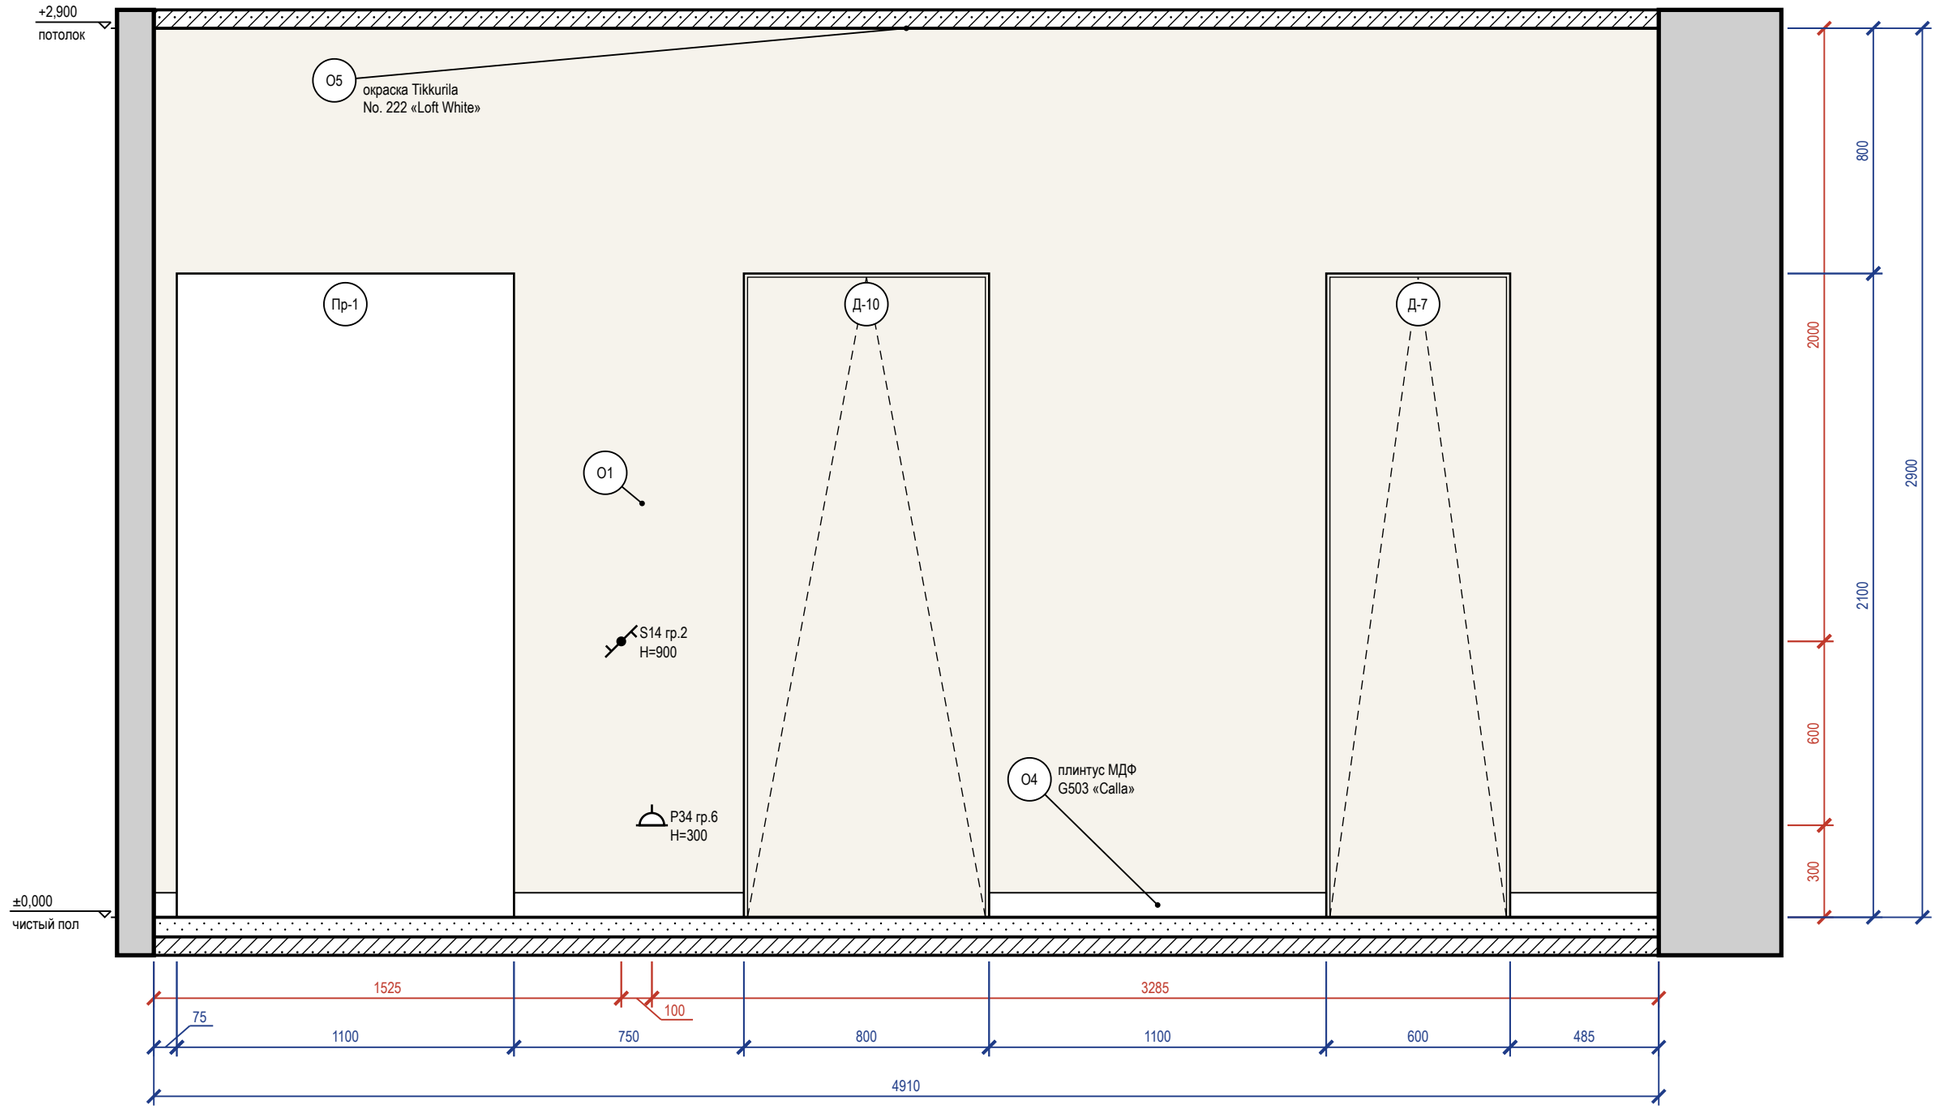


### Схема развёрток (М 1:100)

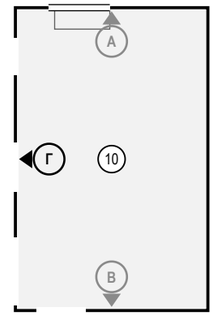


### Ведомость отделки (на листе)

| Марка | Поверхность | Материал, изделие | Цвет, код | Кол. |
|---|---|---|---|---|
| О1 | стены | окраска, Farrow & Ball Modern Emulsion, матовая, подготовка Q3 | Tikkurila G503 «Calla» | 9 м² |
| О4 | плинтус | плинтус МДФ, h 80 мм, аналог: плинтус МДФ под покраску 80×16 | Tikkurila G503 «Calla» | 2,4 м |
| О5 | потолок | окраска, Tikkurila Anti-Reflex 2, глубокоматовая, подготовка Q3 | Little Greene No. 222 «Loft White» | 15,5 м² |

### Примечания


1. Размеры — в мм от чистовых поверхностей стен; условные обозначения и общие указания — лист 2.
2. Двери скрытого монтажа — полотно в плоскости стены, отделка стены по полотну, плинтус прерывается у короба (узел — на листе узлов).

| | | | | | |
|---|---|---|---|---|---|
| | | | | | Проект: Дом 120 м² |
| | Лист | № док. | Подпись | Дата | Развёртка стены Г. Холл второго этажа (пом. 10) |
| Дизайнер | Кырлан А.С. | | | 19.10.26 | |


| Стадия | Лист | Листов |
|---|---|---|
| П | 82 | 104 |

выпуск 19.10.2026 № 46d0102a0d · стр. 82 из 104


## Развёртка стены А

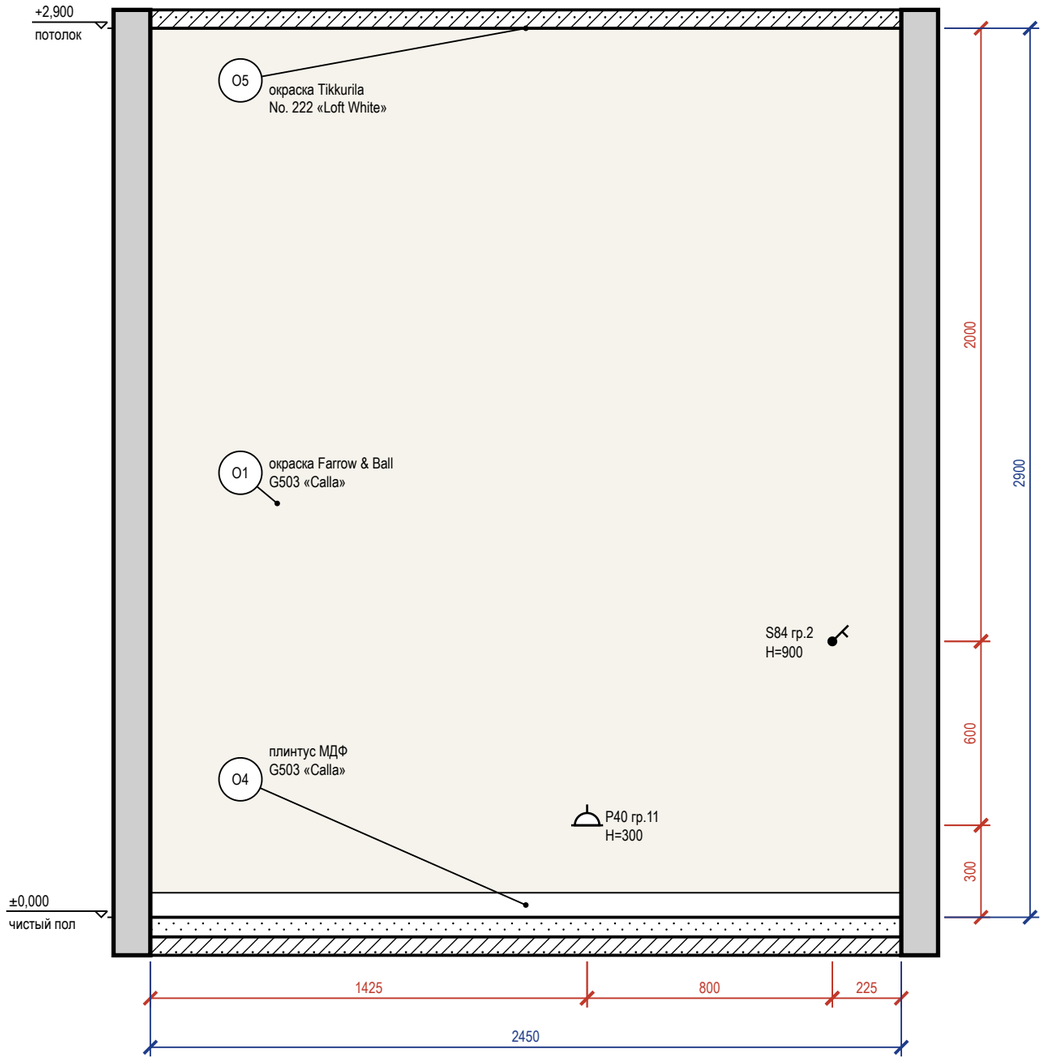


## Развёртка стены В

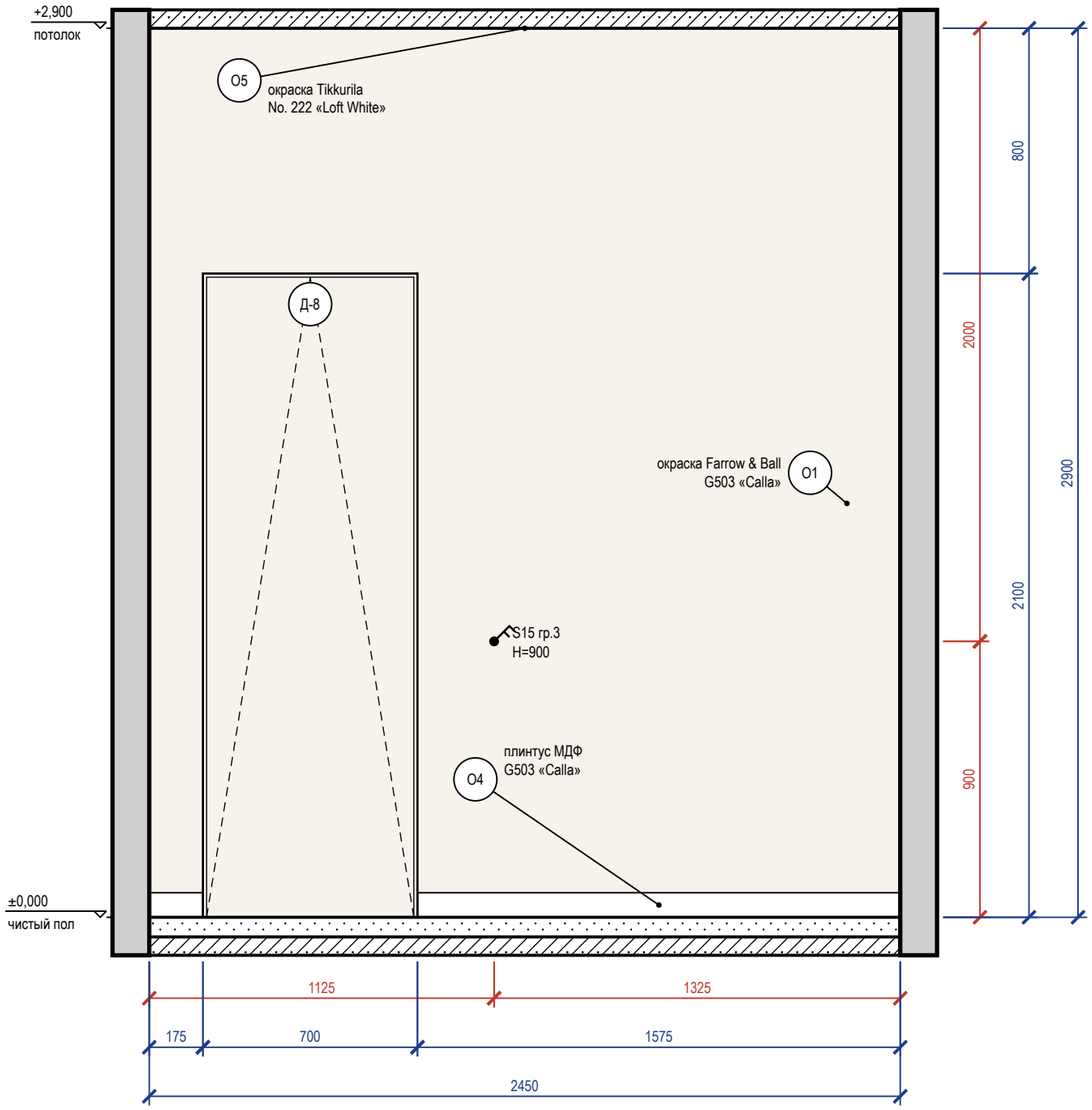


### Схема развёрток (М 1:100)

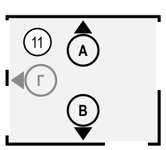


### Ведомость отделки (на листе)

| Марка | Поверхность | Материал, изделие | Цвет, код | Кол. |
|---|---|---|---|---|
| О1 | стены | окраска, Farrow & Ball Modern Emulsion, матовая, подготовка Q3 | Tikkurila G503 «Calla» | 12,7 м² |
| О4 | плинтус | плинтус МДФ, h 80 мм, аналог: плинтус МДФ под покраску 80×16 | Tikkurila G503 «Calla» | 4,2 м |
| О5 | потолок | окраска, Tikkurila Anti-Reflex 2, глубокоматовая, подготовка Q3 | Little Greene No. 222 «Loft White» | 5,2 м² |

### Примечания


1. Размеры — в мм от чистовых поверхностей стен; условные обозначения и общие указания — лист 2.
2. Двери скрытого монтажа — полотно в плоскости стены, отделка стены по полотну, плинтус прерывается у короба (узел — на листе узлов).

| | | | | | |
|---|---|---|---|---|---|
| | | | | | Проект: Дом 120 м² |
| | Лист | № док. | Подпись | Дата | Развёртки стен А, В. Коридор второго этажа (пом. 11) |
| Дизайнер | Кырлан А.С. | | | 19.10.26 | |


| Стадия | Лист | Листов |
|---|---|---|
| П | 83 | 104 |

выпуск 19.10.2026 № 46d0102a0d · стр. 83 из 104

## Развёртка стены Г

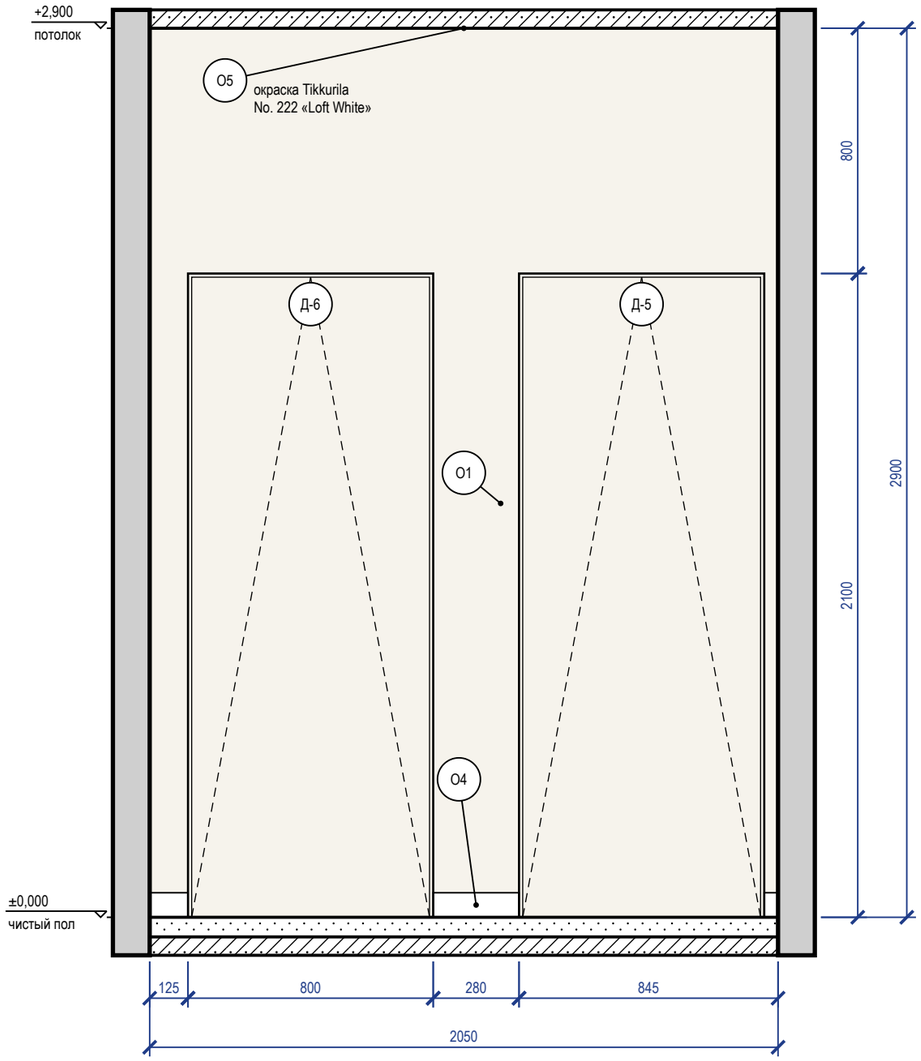


## Схема развёрток (М 1:100)

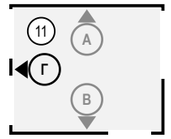


## Ведомость отделки (на листе)

| Марка | Поверхность | Материал, изделие | Цвет, код | Кол. |
|---|---|---|---|---|
| О1 | стены | окраска, Farrow & Ball Modern Emulsion, матовая, подготовка Q3 | Tikkurila G503 «Calla» | 2,6 м² |
| О4 | плинтус | плинтус МДФ, h 80 мм, аналог: плинтус МДФ под покраску 80×16 | Tikkurila G503 «Calla» | 0,5 м |
| О5 | потолок | окраска, Tikkurila Anti-Reflex 2, глубокоматовая, подготовка Q3 | Little Greene No. 222 «Loft White» | 5,2 м² |

## Примечания


1. Размеры — в мм от чистовых поверхностей стен; условные обозначения и общие указания — лист 2.
2. Двери скрытого монтажа — полотно в плоскости стены, отделка стены по полотну, плинтус прерывается у короба (узел — на листе узлов).

| | | | | | |
|---|---|---|---|---|---|
| | | | | | Проект: Дом 120 м² |
| | Лист | № док. | Подпись | Дата | Развёртка стены Г. Коридор второго этажа (пом. 11) |
| Дизайнер | Кырлан А.С. | | | 19.10.26 | |


| Стадия | Лист | Листов |
|---|---|---|
| П | 84 | 104 |

выпуск 19.10.2026 № 46d0102a0d · стр. 84 из 104

## Развёртка стены А

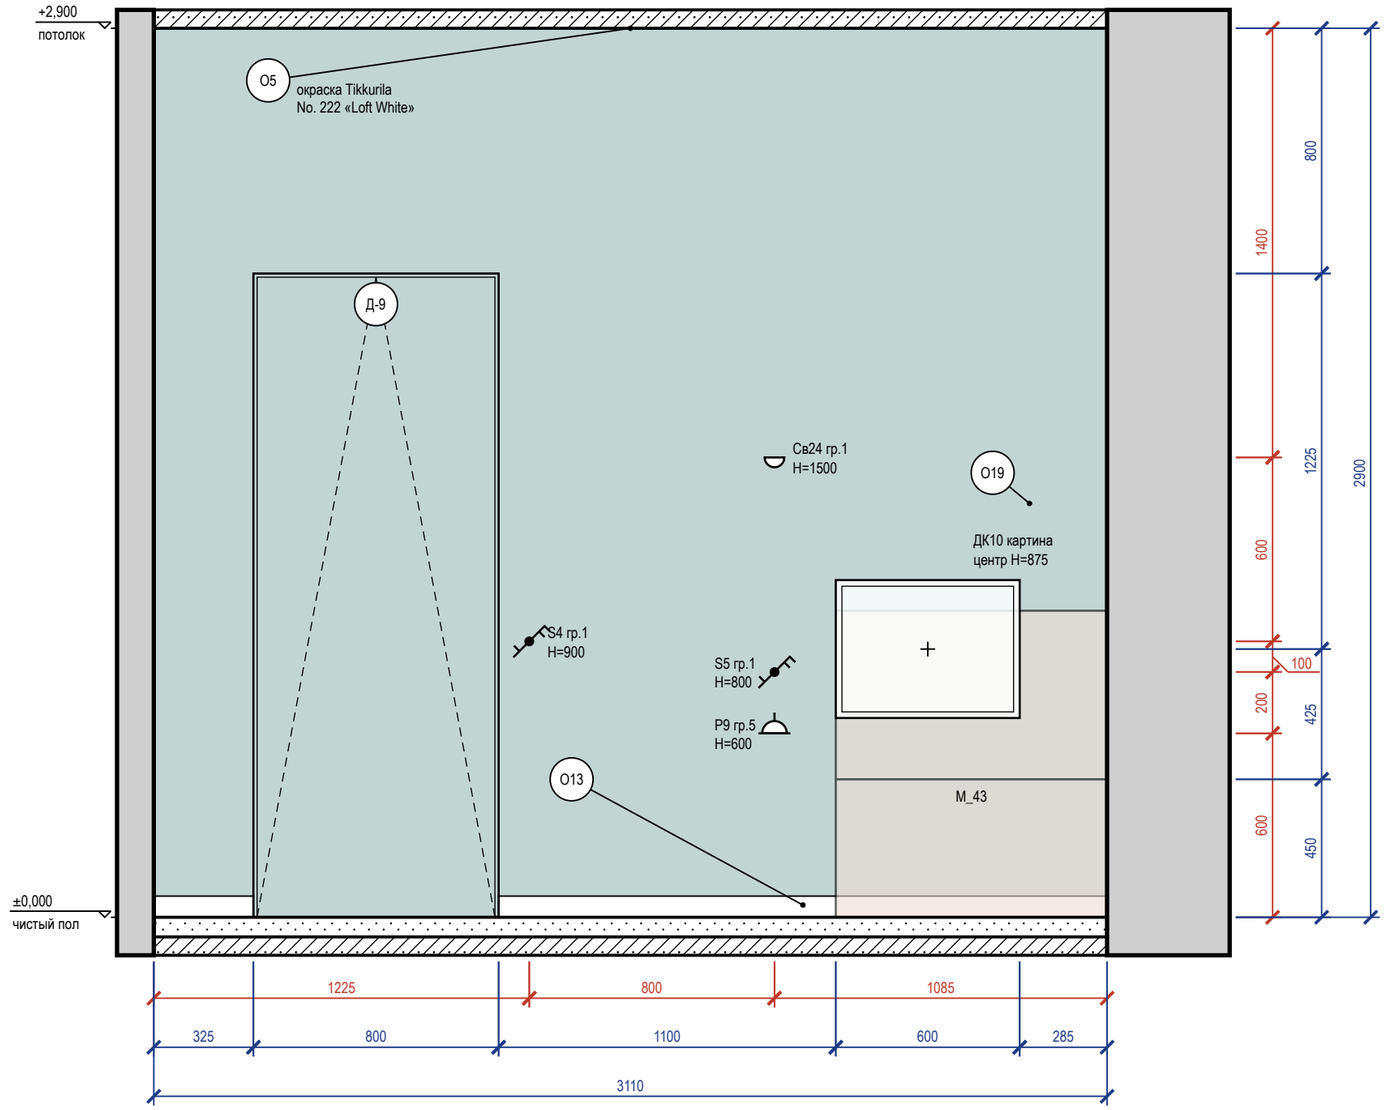


### Схема развёрток (М 1:100)

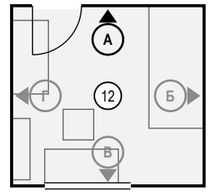


### Ведомость отделки (на листе)

| Марка | Поверхность | Материал, изделие | Цвет, код | Кол. |
|---|---|---|---|---|
| О5 | потолок | окраска, Tikkurila Anti-Reflex 2, глубокоматовая, подготовка Q3 | Little Greene No. 222 «Loft White» | 9,2 м² |
| О13 | плинтус | плинтус МДФ, Orac Decor Contour (Luxxus), h 69 мм, SX165 | Tikkurila G503 «Calla» | 2,3 м |
| О19 | акцентная стена | окраска, Farrow & Ball Modern Emulsion, матовая, подготовка Q3 | Tikkurila H440 «H440 Wave бирюзово-голубая вода» | 7,3 м² |

### Примечания


1. Размеры — в мм от чистовых поверхностей стен; условные обозначения и общие указания — лист 2.
2. Картины и зеркала крепить к основанию по паспорту изделия (закладные и анкеры — в перечне скрытых работ); крест — ось центра предмета.
3. Двери скрытого монтажа — полотно в плоскости стены, отделка стены по полотну, плинтус прерывается у короба (узел — на листе узлов).

| | | | | | |
|---|---|---|---|---|---|
| | | | | | Проект: Дом 120 м² |
| | Лист | № док. | Подпись | Дата | |
| Дизайнер | Кырлан А.С. | | | 19.10.26 | Развёртка стены А. Детская вторая (пом. 12) |


| Стадия | Лист | Листов |
|---|---|---|
| П | 85 | 104 |

выпуск 19.10.2026 № 46d0102a0d · стр. 85 из 104

## Развёртка стены Б

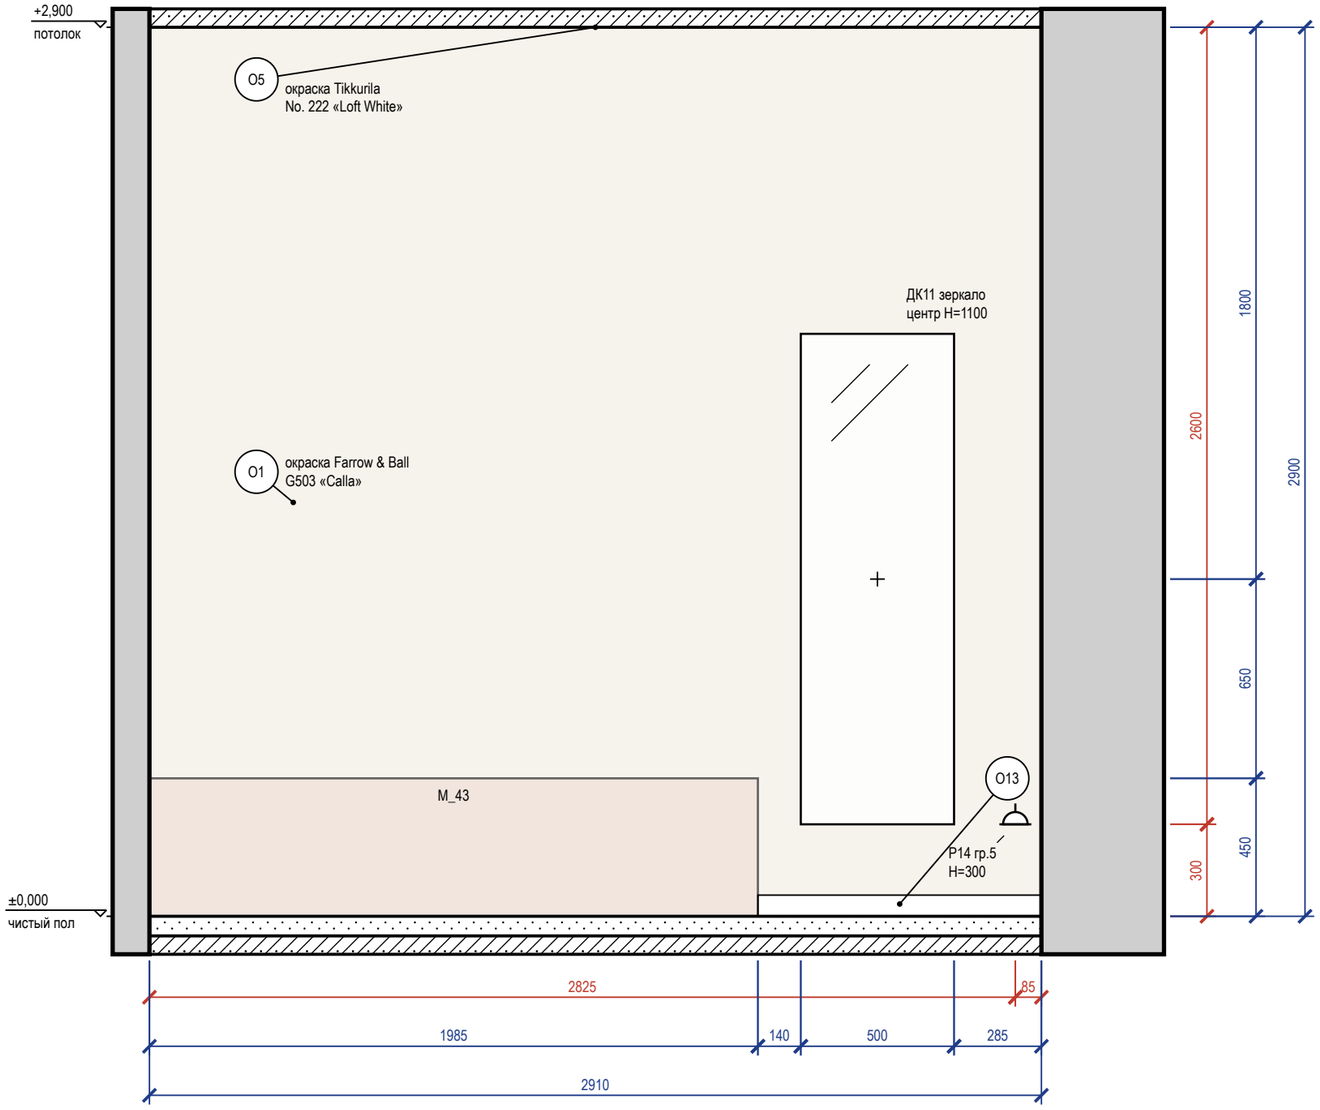


## Схема развёрток (М 1:100)

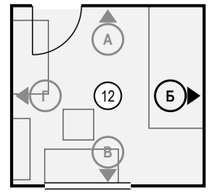


## Ведомость отделки (на листе)

| Марка | Поверхность | Материал, изделие | Цвет, код | Кол. |
|---|---|---|---|---|
| О1 | стены | окраска, Farrow & Ball Modern Emulsion, матовая, подготовка Q3 | Tikkurila G503 «Calla» | 8,4 м² |
| О5 | потолок | окраска, Tikkurila Anti-Reflex 2, глубокоматовая, подготовка Q3 | Little Greene No. 222 «Loft White» | 9,2 м² |
| О13 | плинтус | плинтус МДФ, Orac Decor Contour (Luxxus), h 69 мм, SX165 | Tikkurila G503 «Calla» | 0,9 м |

### Примечания


1. Размеры — в мм от чистовых поверхностей стен; условные обозначения и общие указания — лист 2.
2. Картины и зеркала крепить к основанию по паспорту изделия (закладные и анкеры — в перечне скрытых работ); крест — ось центра предмета.

| | | | | | |
|---|---|---|---|---|---|
| | | | | | Проект: Дом 120 м² |
| | Лист | № док. | Подпись | Дата | Развёртка стены Б. Детская вторая (пом. 12) |
| Дизайнер | Кырлан А.С. | | | 19.10.26 | |


| Стадия | Лист | Листов |
|---|---|---|
| П | 86 | 104 |

выпуск 19.10.2026 № 46d0102a0d · стр. 86 из 104

## Развёртка стены В

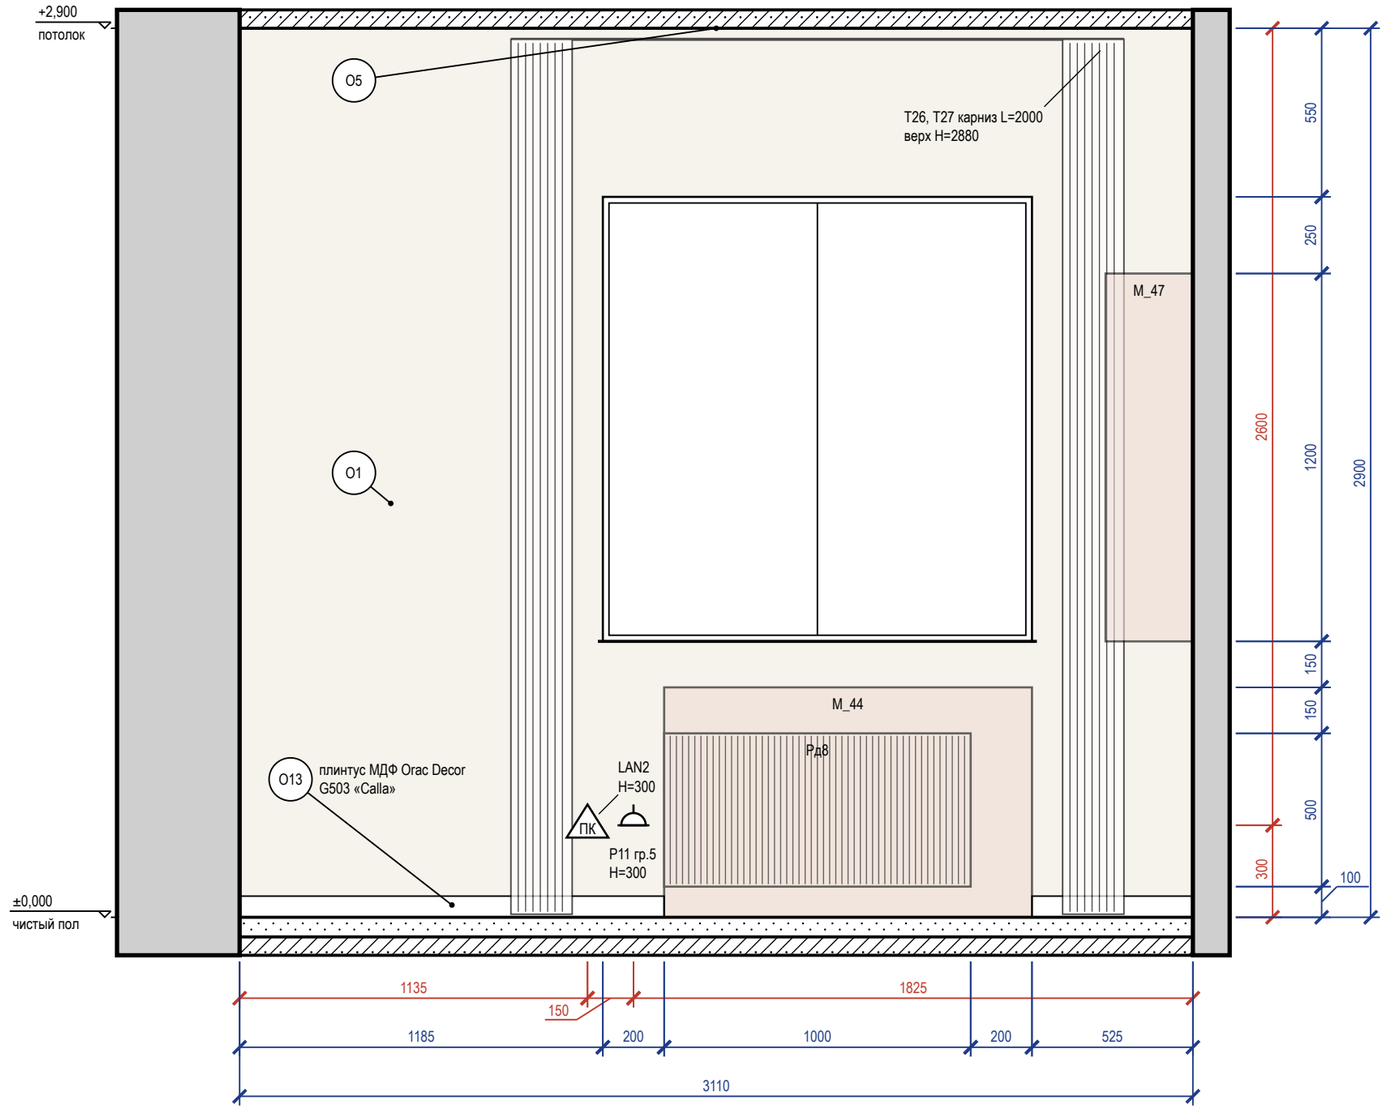


## Схема развёрток (М 1:100)

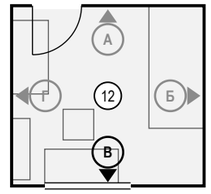


## Ведомость отделки (на листе)

| Марка | Поверхность | Материал, изделие | Цвет, код | Кол. |
|---|---|---|---|---|
| О1 | стены | окраска, Farrow & Ball Modern Emulsion, матовая, подготовка Q3 | Tikkurila G503 «Calla» | 7 м² |
| О5 | потолок | окраска, Tikkurila Anti-Reflex 2, глубокоматовая, подготовка Q3 | Little Greene No. 222 «Loft White» | 9,2 м² |
| О13 | плинтус | плинтус МДФ, Orac Decor Contour (Luxxus), h 69 мм, SX165 | Tikkurila G503 «Calla» | 1,9 м |

### Примечания


1. Размеры — в мм от чистовых поверхностей стен; условные обозначения и общие указания — лист 2.
2. Карнизы (шины) — по ведомости текстиля декоратора; длина L и верх Н — по развёртке, крепление — до окраски потолка.

| | | | | | |
|---|---|---|---|---|---|
| | Лист | № док. | Подпись | Дата | Проект: Дом 120 м² |
| Дизайнер | Кырлан А.С. | | | 19.10.26 | Развёртка стены В. Детская вторая (пом. 12) |


| Стадия | Лист | Листов |
|---|---|---|
| П | 87 | 104 |

выпуск 19.10.2026 № 46d0102a0d · стр. 87 из 104

## Развёртка стены Г

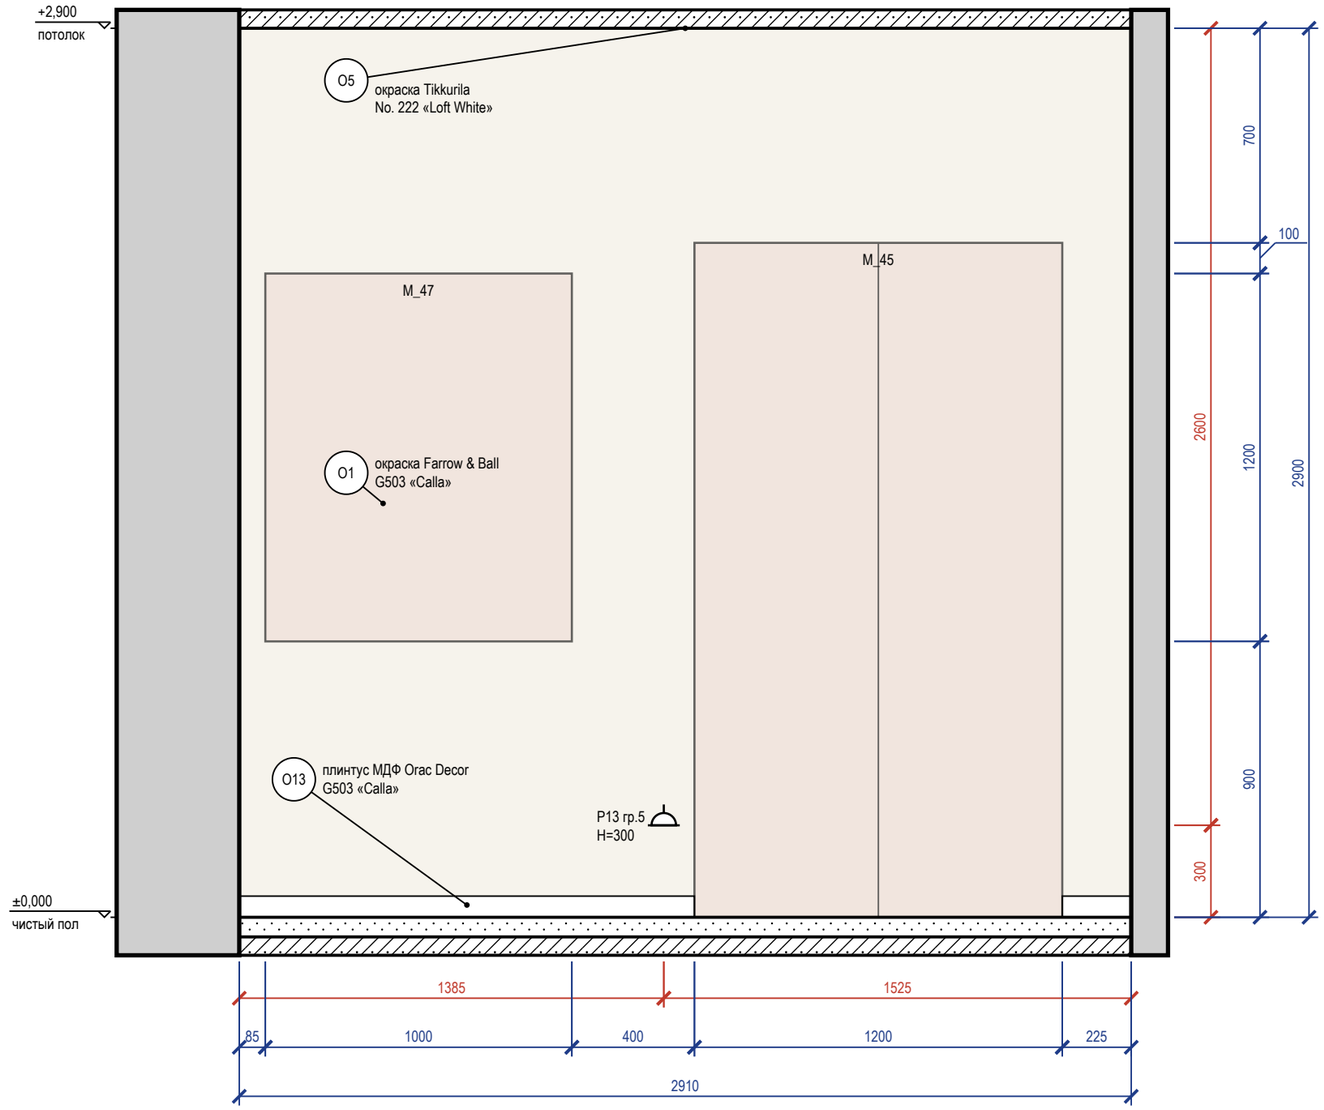


### Схема развёрток (М 1:100)

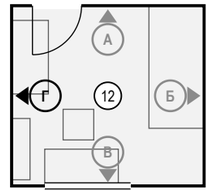


### Ведомость отделки (на листе)

| Марка | Поверхность | Материал, изделие | Цвет, код | Кол. |
|---|---|---|---|---|
| О1 | стены | окраска, Farrow & Ball Modern Emulsion, матовая, подготовка Q3 | Tikkurila G503 «Calla» | 8,4 м² |
| О5 | потолок | окраска, Tikkurila Anti-Reflex 2, глубокоматовая, подготовка Q3 | Little Greene No. 222 «Loft White» | 9,2 м² |
| О13 | плинтус | плинтус МДФ, Orac Decor Contour (Luxxus), h 69 мм, SX165 | Tikkurila G503 «Calla» | 1,7 м |

### Примечания


1. Размеры — в мм от чистовых поверхностей стен; условные обозначения и общие указания — лист 2.

| | | | | | |
|---|---|---|---|---|---|
| | Лист | № док. | Подпись | Дата | Проект: Дом 120 м² |
| Дизайнер | Кырлан А.С. | | | 19.10.26 | Развёртка стены Г. Детская вторая (пом. 12) |


| Стадия | Лист | Листов |
|---|---|---|
| П | 88 | 104 |

выпуск 19.10.2026 № 46d0102a0d · стр. 88 из 104


## Развёртка стены А

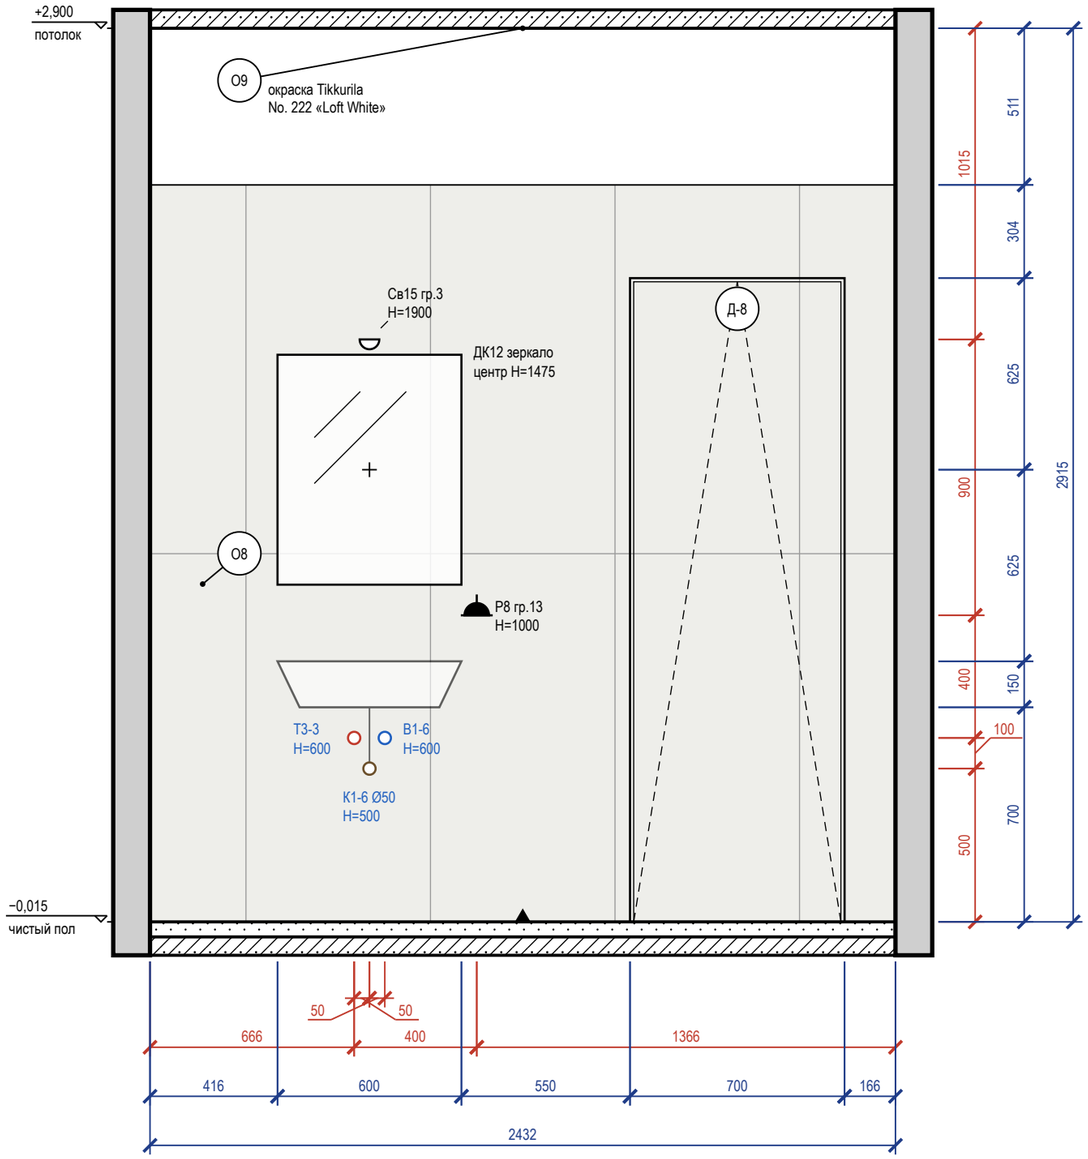


## Развёртка стены Б

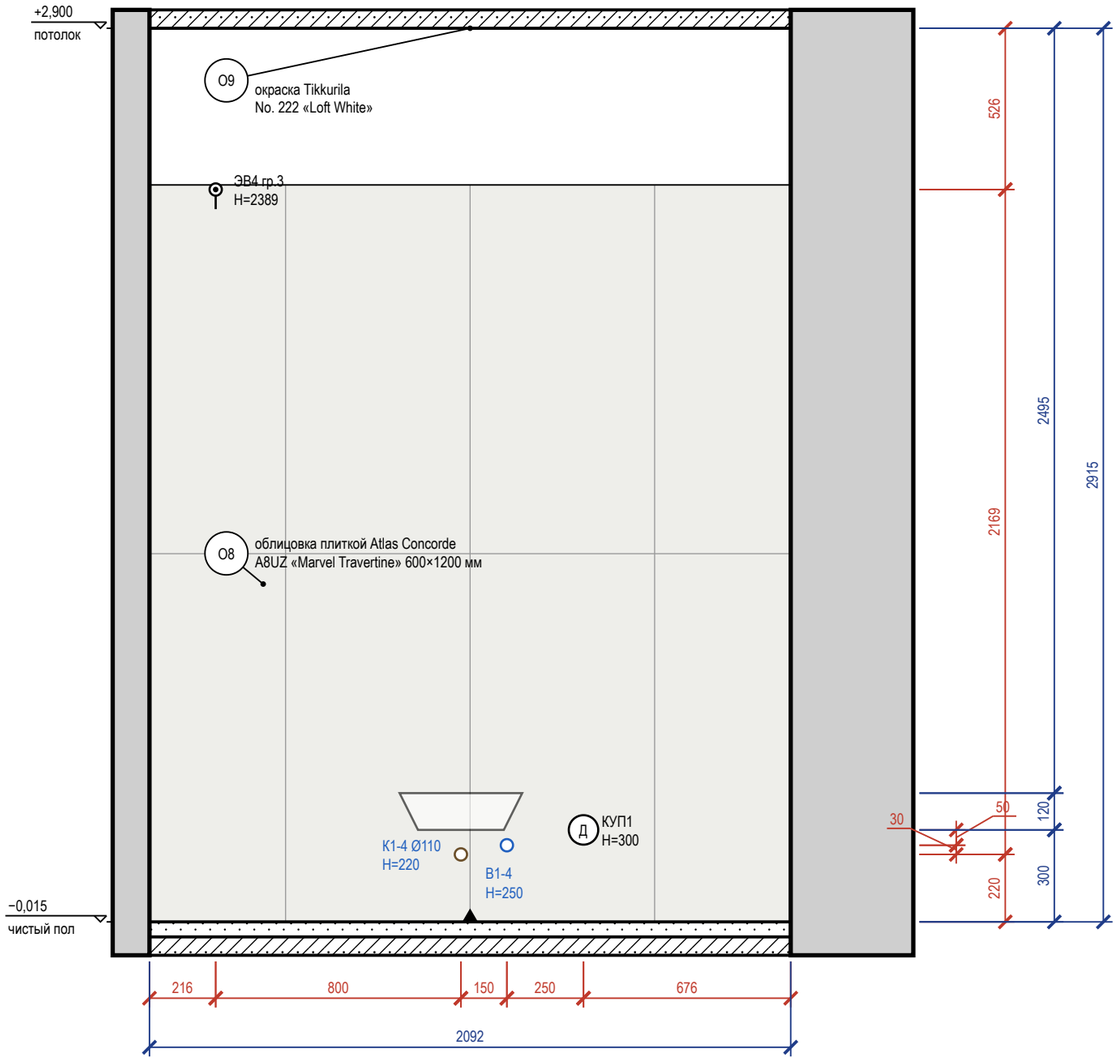


### Схема развёрток (М 1:100)

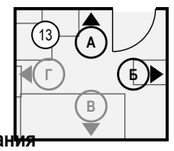


### Ведомость отделки (на листе)

| Марка | Поверхность | Материал, изделие | Цвет, код | Кол. |
|---|---|---|---|---|
| О8 | стены | облицовка плиткой, Atlas Concorde Marvel Travertine, 600×1200×9 мм, A8UZ, затирка CG2WA | Atlas Concorde A8UZ «Marvel Travertine» | 9,4 м² |
| О9 | потолок | окраска, Tikkurila Luja 7, матовая, подготовка Q3 | Little Greene No. 222 «Loft White» | 5,3 м² |

### Примечания


1. Размеры — в мм от чистовых поверхностей стен; условные обозначения и общие указания — лист 2.
2. Схема мебели, приборов и декора не является технической документацией для производства мебели; габариты — по паспортам изделий.
3. Выводы ВК — коды и высоты по листу выводов сантехники.
4. Облицовка — по сетке швов 2 мм, раскладка от оси стены (треугольник у пола), целые ряды от пола; подрезки — по листу раскладки плитки.
5. Гидроизоляция в 2 слоя, заход на стены 200 мм — до облицовки, с актом скрытых работ и тестом проливом (узел — на листе узлов).
6. Картины и зеркала крепить к основанию по паспорту изделия (закладные и анкеры — в перечне скрытых работ); крест — ось центра предмета.
7. Двери скрытого монтажа — полотно в плоскости стены, отделка стены по полотну, плинтус прерывается у короба (узел — на листе узлов).

| | | | | | |
|---|---|---|---|---|---|
| | | | | | Проект: Дом 120 м² |
| | Лист | № док. | Подпись | Дата | Развёртки стен А, Б. Санузел второго этажа (пом. 13) |
| Дизайнер | Кырлан А.С. | | | 19.10.26 | |


| Стадия | Лист | Листов |
|---|---|---|
| П | 89 | 104 |

выпуск 19.10.2026 № 46d0102a0d · стр. 89 из 104


## Развёртка стены В

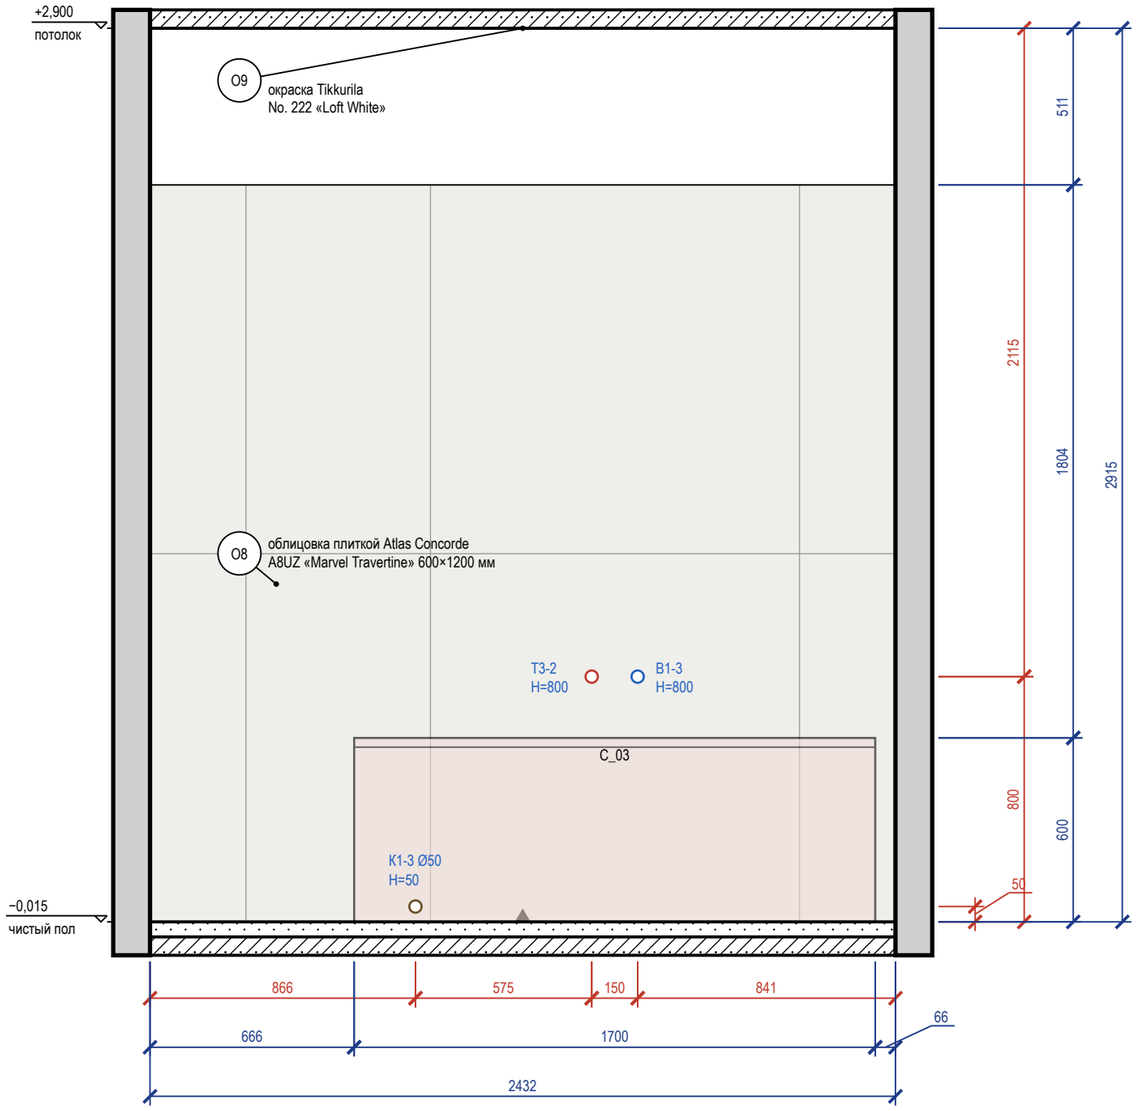


## Развёртка стены Г

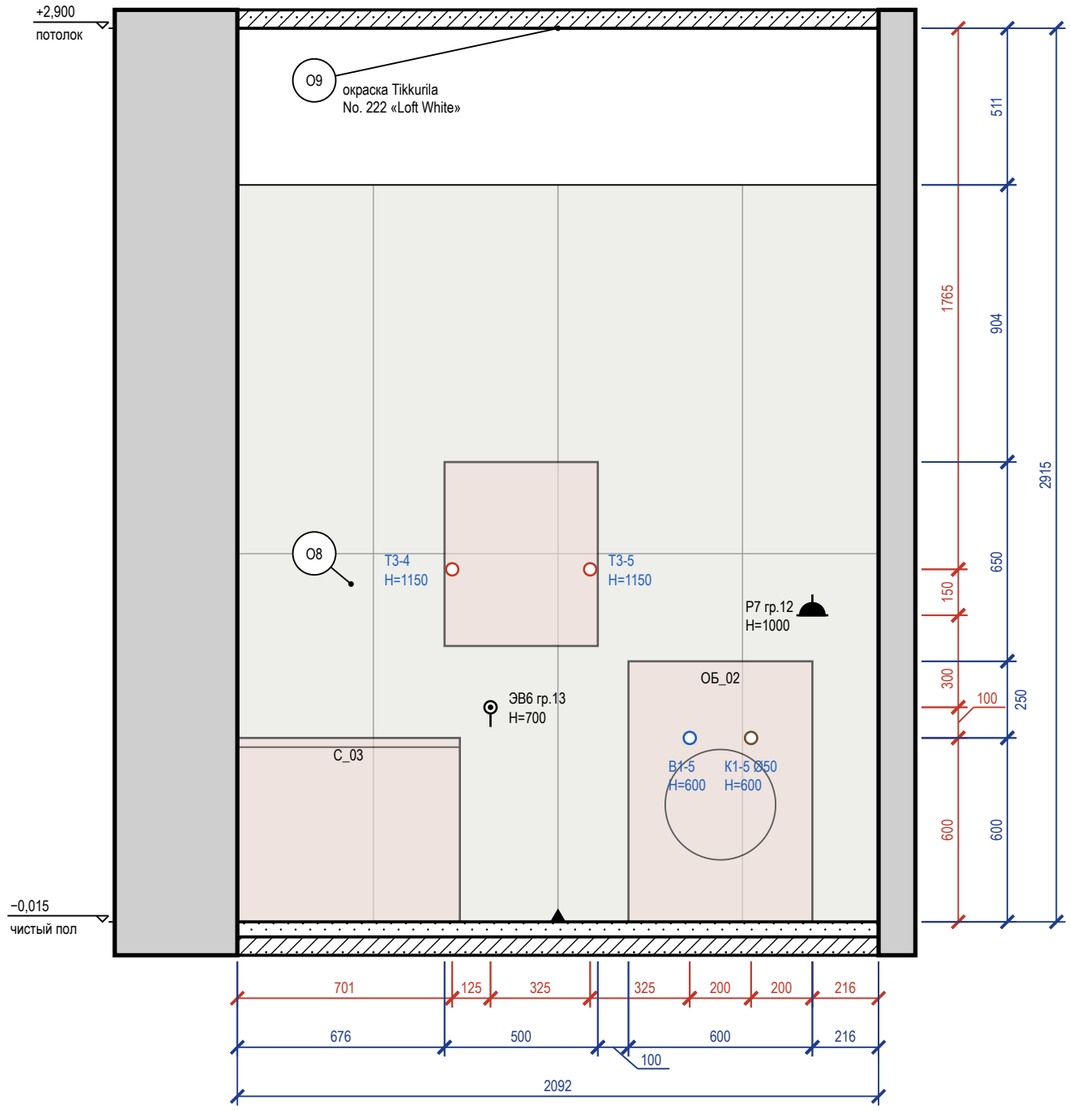


### Схема развёрток (М 1:100)

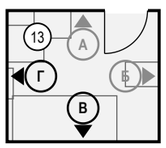


### Ведомость отделки (на листе)

| Марка | Поверхность | Материал, изделие | Цвет, код | Кол. |
|---|---|---|---|---|
| О8 | стены | облицовка плиткой, Atlas Concorde Marvel Travertine, 600×1200×9 мм, A8UZ, затирка CG2WA | Atlas Concorde A8UZ «Marvel Travertine» | 10,9 м² |
| О9 | потолок | окраска, Tikkurila Luja 7, матовая, подготовка Q3 | Little Greene No. 222 «Loft White» | 5,3 м² |

### Примечания


1. Размеры — в мм от чистовых поверхностей стен; условные обозначения и общие указания — лист 2.
2. Схема мебели, приборов и декора не является технической документацией для производства мебели; габариты — по паспортам изделий.
3. Выводы ВК — коды и высоты по листу выводов сантехники.
4. Облицовка — по сетке швов 2 мм, раскладка от оси стены (треугольник у пола), целые ряды от пола; подрезки — по листу раскладки плитки.
5. Гидроизоляция в 2 слоя, заход на стены 200 мм — до облицовки, с актом скрытых работ и тестом проливом (узел — на листе узлов).

| | | | | | |
|---|---|---|---|---|---|
| | | | | | Проект: Дом 120 м² |
| | Лист | № док. | Подпись | Дата | Развёртки стен В, Г. Санузел второго этажа (пом. 13) |
| Дизайнер | Кырлан А.С. | | | 19.10.26 | |


| Стадия | Лист | Листов |
|---|---|---|
| П | 90 | 104 |

выпуск 19.10.2026 № 46d0102a0d · стр. 90 из 104


## Вид с фасадами

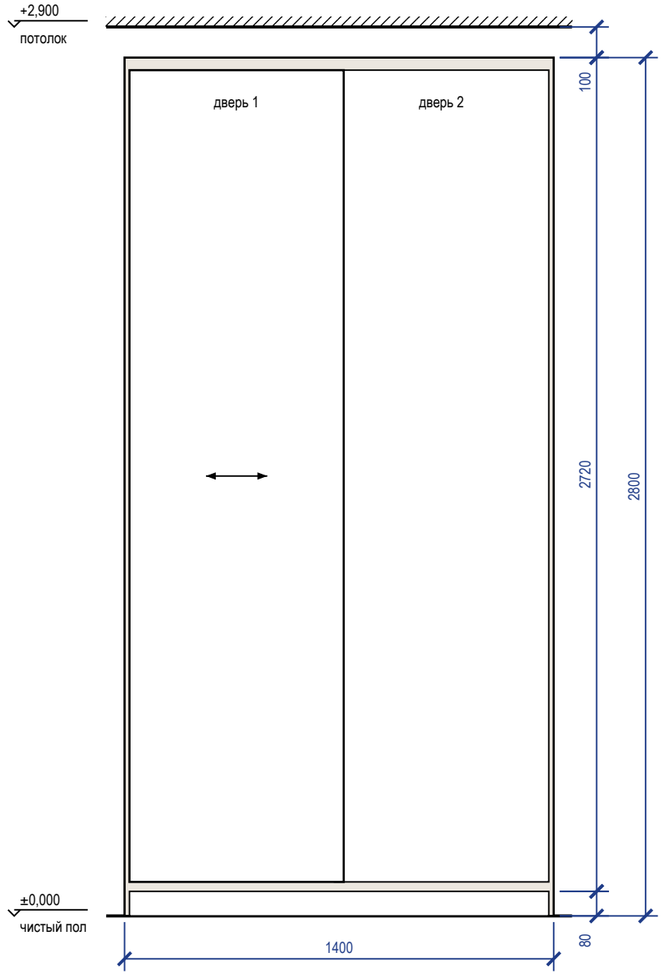



## Вид без фасадов

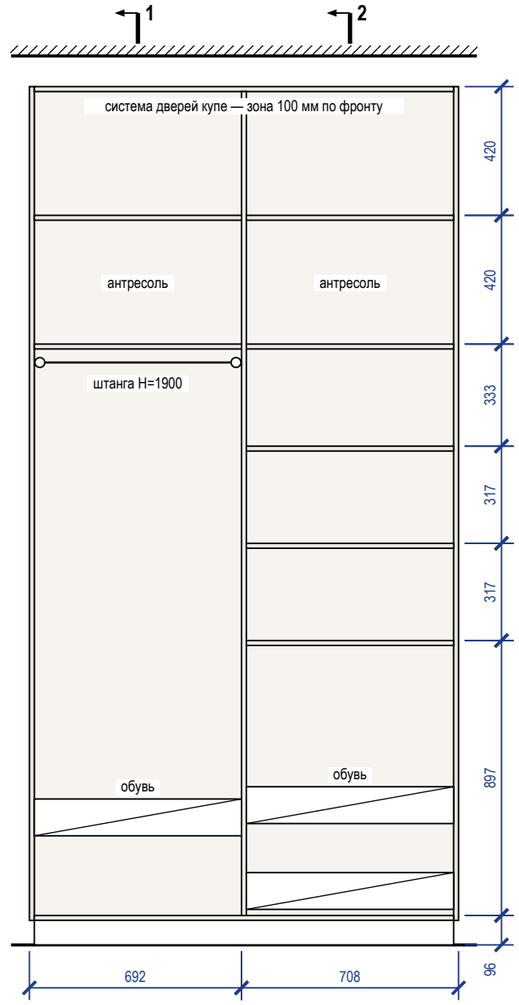


## Разрез 1-1

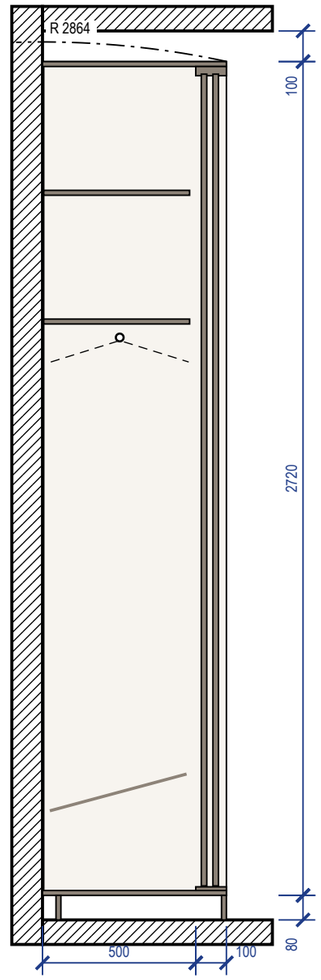



## Разрез 2-2

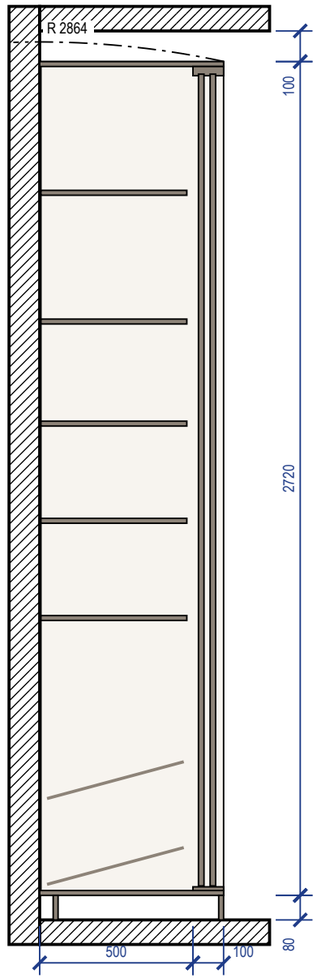


### Примечания

1. Размеры — в мм по чистовой отделке; изделие 1400×600×2800 (Ш×Г×В). Перед раскроем — контрольный замер цеха после чистовой отделки стен, пола и потолка.
2. Корпус — ЛДСП 16 мм, задняя стенка ХДФ 4 мм в паз, цоколь 80 мм на регулируемых опорах; двери купе — ЛДСП 10 мм в алюминиевом профиле, нахлёст 30 мм, ширина двери 699 мм, высота — проём минус 40 мм; цвет — по колерной карте.
3. Кромка: скрытые торцы 0,4 мм, видимые 2 мм (ПВХ/АБС).
4. Номинальные зазоры: дверь купе — боковина 3 мм, фасад ящика — стойка 2 мм; ящики внутри купе — с накладкой 30 мм на стойке со стороны нахлёста дверей.
5. Ящики — направляющие полного выдвижения NL 450 (внутренняя глубина 496 мм ≥ NL + 3); присадка по 32-й системе — выполняет цех.
6. Зазор до потолка 100 мм — закрыть планкой в цвет корпуса при монтаже.
7. Подъём корпуса: диагональ боковины $\sqrt{(2800^2 + 600^2)} = 2864$ мм < 2900 мм до потолка — корпус собирается лёжа и поднимается поворотом.
8. Крепление к стене от опрокидывания — уголки 2 шт. к несущему основанию (монтажная схема шкафов).

## 3D орто

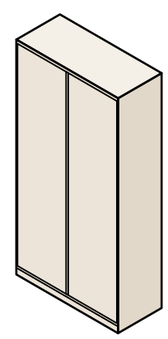


| | | | | | |
|---|---|---|---|---|---|
| | | | | | Проект: Дом 120 м² |
| | Лист | № док. | Подпись | Дата | Шкаф-купе M_25 |
| Дизайнер | Кырлан А.С. | | | 19.10.26 | |


| Стадия | Лист | Листов |
|---|---|---|
| П | Д_1 | 104 |

выпуск 19.10.2026 № 46d0102a0d · стр. 91 из 104


## Вид с фасадами

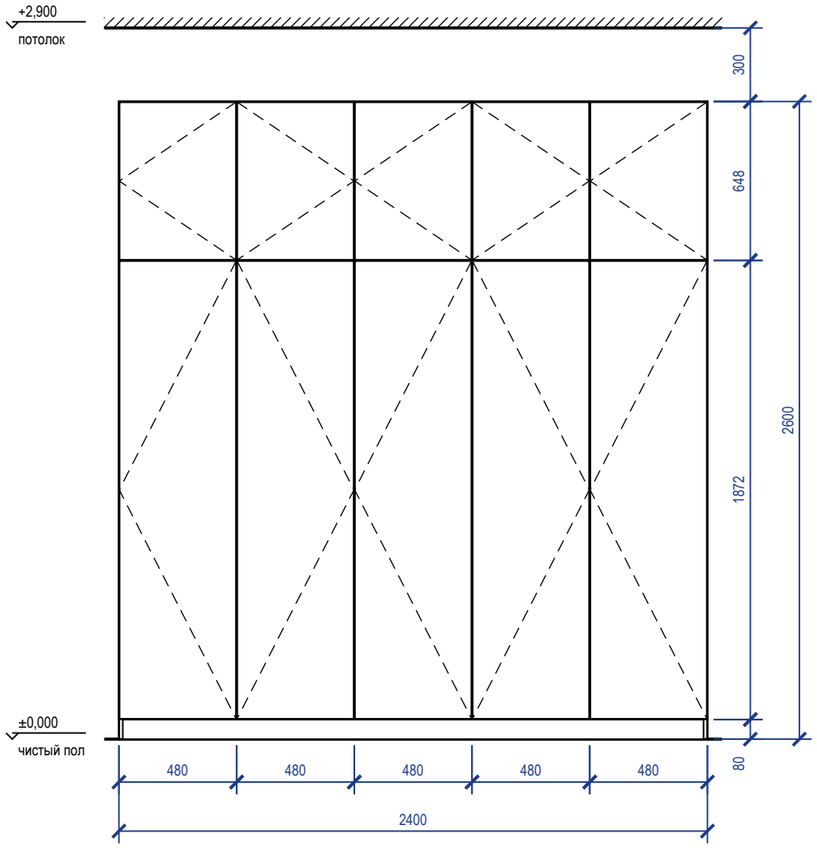



## Вид без фасадов

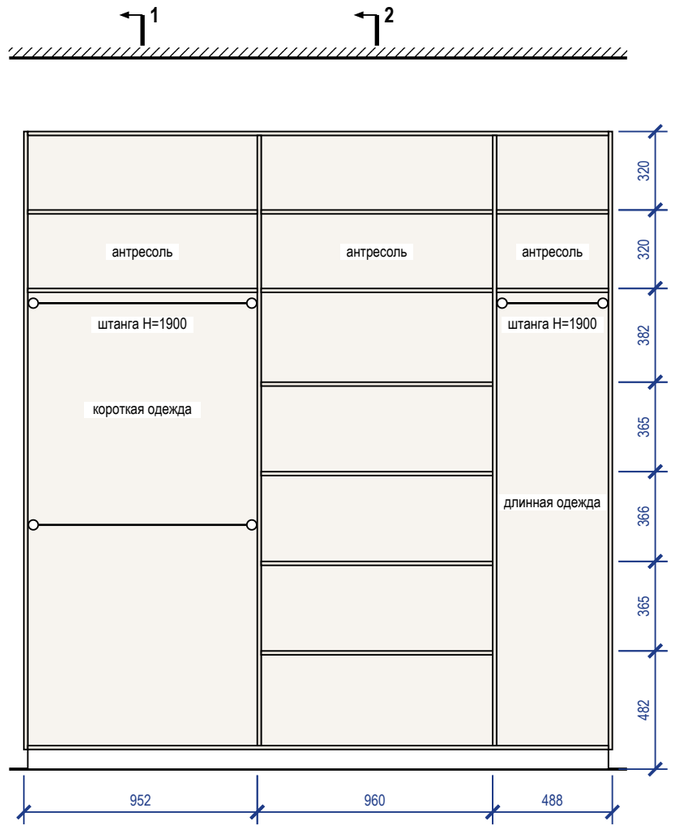


## Разрез 1-1

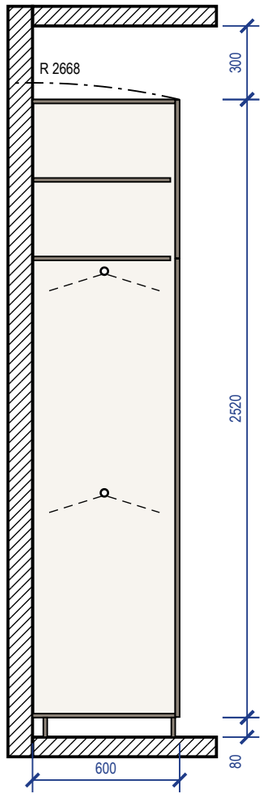



## Разрез 2-2

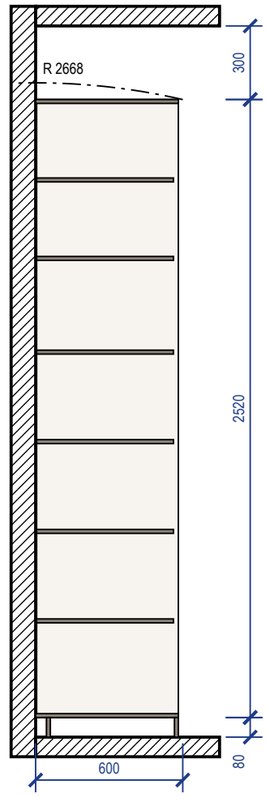


### Примечания

1. Размеры — в мм по чистовой отделке; изделие 2400×600×2600 (Ш×Г×В). Перед раскроем — контрольный замер цеха после чистовой отделки стен, пола и потолка.
2. Корпус — ЛДСП 16 мм, задняя стенка ХДФ 4 мм в паз, цоколь 80 мм на регулируемых опорах; фасады — МДФ, эмаль матовая 18 мм накладные, цвет — по колерной карте; петли с доводчиком: фасад 1869 мм — 4 петли, фасад 645 мм — 2 петли.
3. Кромка: скрытые торцы 0,4 мм, видимые 2 мм (ПВХ/АБС).
4. Номинальные зазоры: между фасадами 3 мм, фасад — стена и фасад — потолок не менее 3 мм, фасад ящика — стойка 2 мм.
5. Ящики — направляющие полного выдвижения NL 550 (внутренняя глубина 578 мм ≥ NL + 3); присадка по 32-й системе — выполняет цех.
6. Зазор до потолка 300 мм.
7. Подъём корпуса: диагональ боковины $\sqrt{(2600^2 + 600^2)} = 2668$ мм < 2900 мм до потолка — корпус собирается лёжа и поднимается поворотом.
8. Крепление к стене от опрокидывания — уголки 2 шт. к несущему основанию (монтажная схема шкафов).

## 3D орто

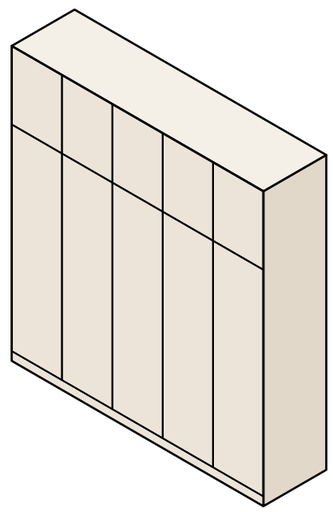


| | | | | | |
|---|---|---|---|---|---|
| | | | | | Проект: Дом 120 м² |
| | Лист | № док. | Подпись | Дата | |
| Дизайнер | Кырлан А.С. | | | 19.10.26 | Шкаф распашной M_30 |


| Стадия | Лист | Листов |
|---|---|---|
| П | Д_2 | 104 |

выпуск 19.10.2026 № 46d0102a0d · стр. 92 из 104


## Вид с фасадами

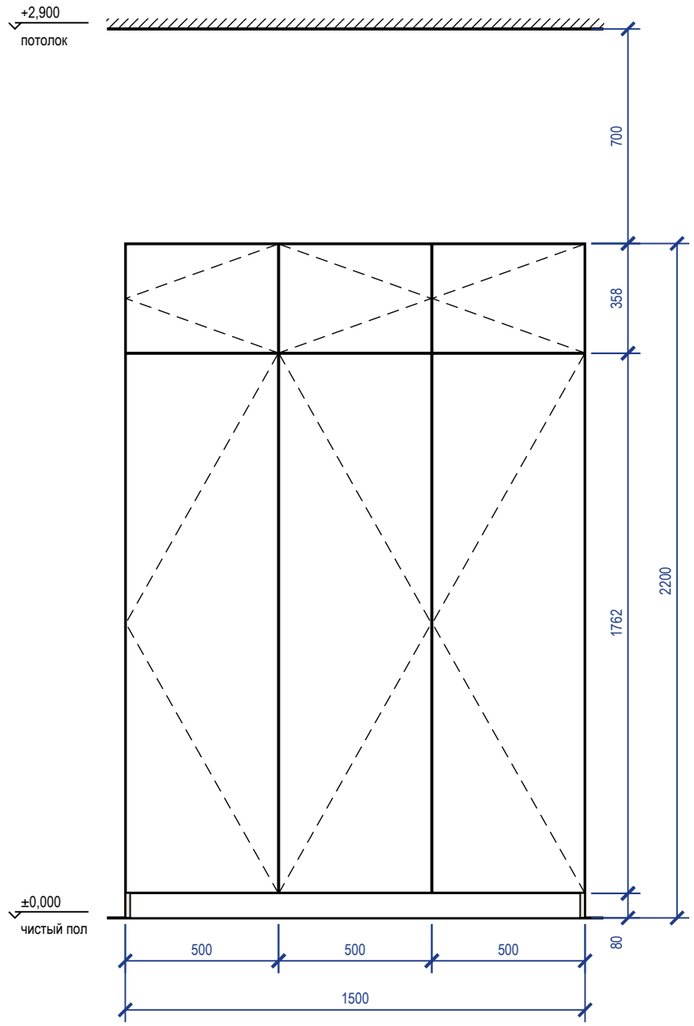



## Вид без фасадов

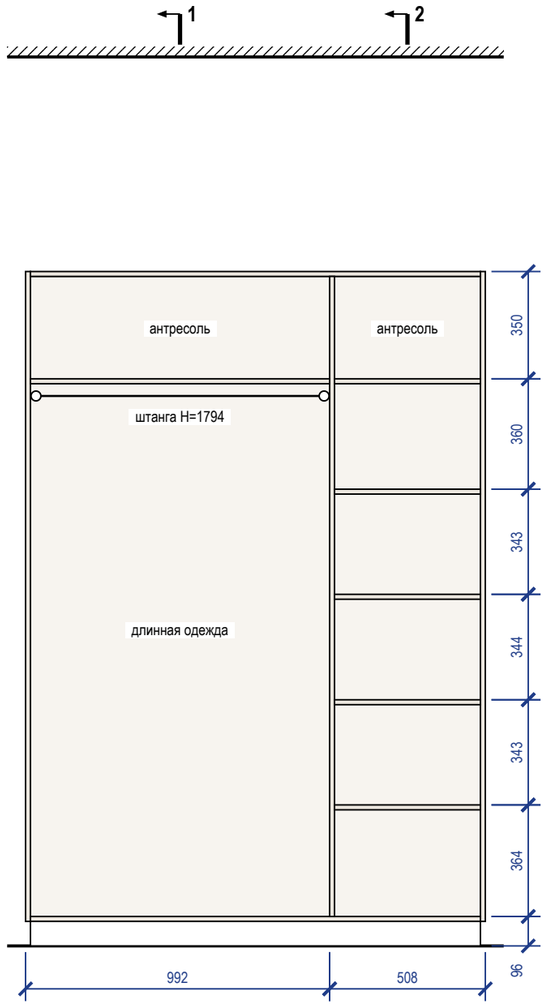


## Разрез 1-1

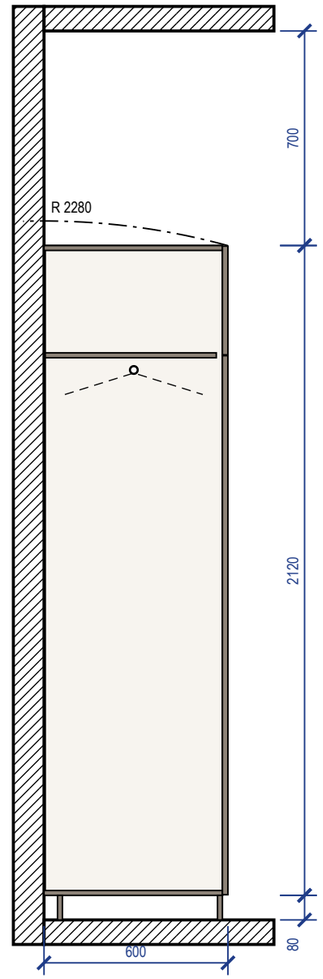



## Разрез 2-2

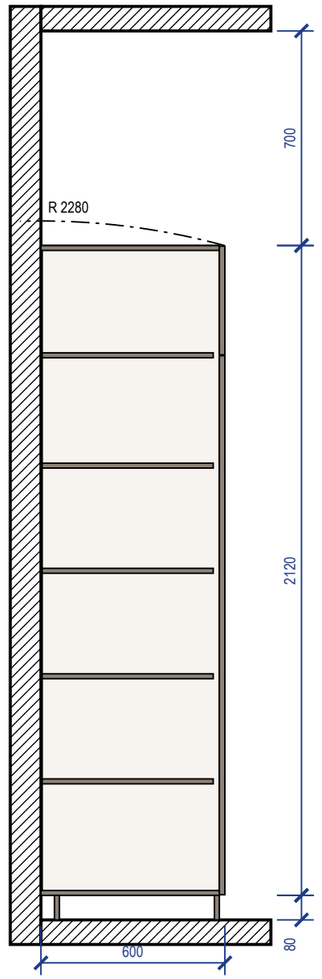


## Примечания

1. Размеры — в мм по чистовой отделке; изделие 1500×600×2200 (Ш×Г×В). Перед раскроем — контрольный замер цеха после чистовой отделки стен, пола и потолка.
2. Корпус — ЛДСП 16 мм, задняя стенка ХДФ 4 мм в паз, цоколь 80 мм на регулируемых опорах; фасады — МДФ, эмаль матовая 18 мм накладные, цвет — по колерной карте; петли с доводчиком: фасад 1759 мм — 4 петли, фасад 355 мм — 2 петли.
3. Кромка: скрытые торцы 0,4 мм, видимые 2 мм (ПВХ/АБС).
4. Номинальные зазоры: между фасадами 3 мм, фасад — стена и фасад — потолок не менее 3 мм, фасад ящика — стойка 2 мм.
5. Ящики — направляющие полного выдвижения NL 550 (внутренняя глубина 578 мм ≥ NL + 3); присадка по 32-й системе — выполняет цех.
6. Зазор до потолка 700 мм.
7. Подъём корпуса: диагональ боковины $\sqrt{(2200^2 + 600^2)} = 2280$ мм < 2900 мм до потолка — корпус собирается лёжа и поднимается поворотом.
8. Крепление к стене от опрокидывания — уголки 2 шт. к несущему основанию (монтажная схема шкафов).


## 3D орто

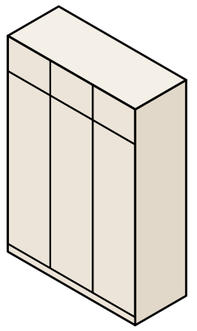


| | | | | | | |
|---|---|---|---|---|---|---|
| | | | | | Проект: Дом 120 м² | |
| | Лист | № док. | Подпись | Дата | | |
| Дизайнер | Кырлан А.С. | | | 19.10.26 | Шкаф распашной M_35 | Стадия: П; Лист: Д_3; Листов: 104 |

выпуск 19.10.2026 № 46d0102a0d · стр. 93 из 104


**Общий вид**

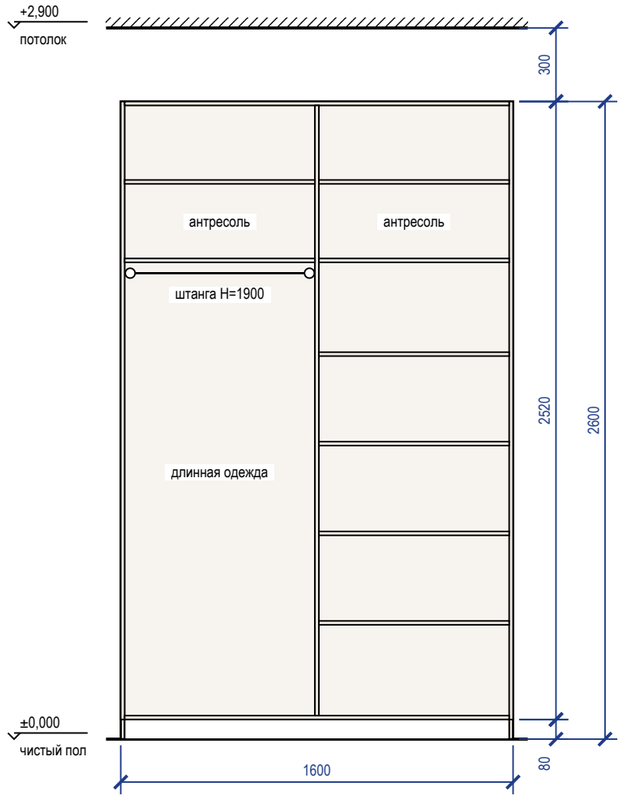



**Наполнение, размеры в свету**

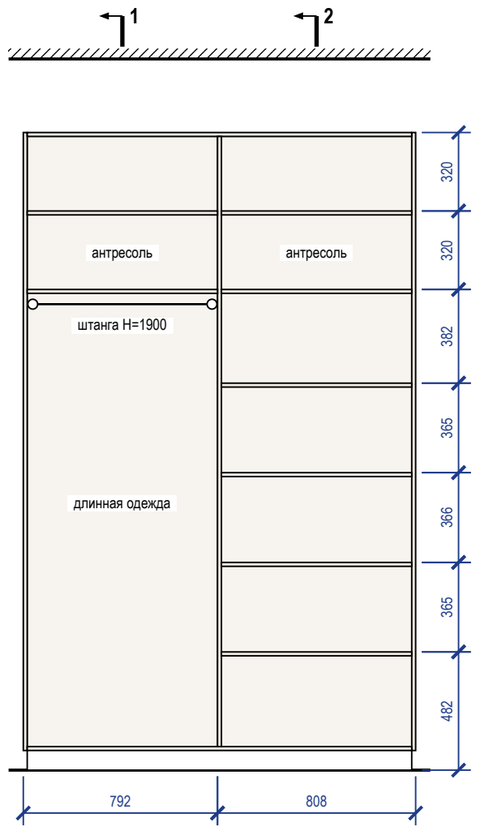


**Разрез 1-1**

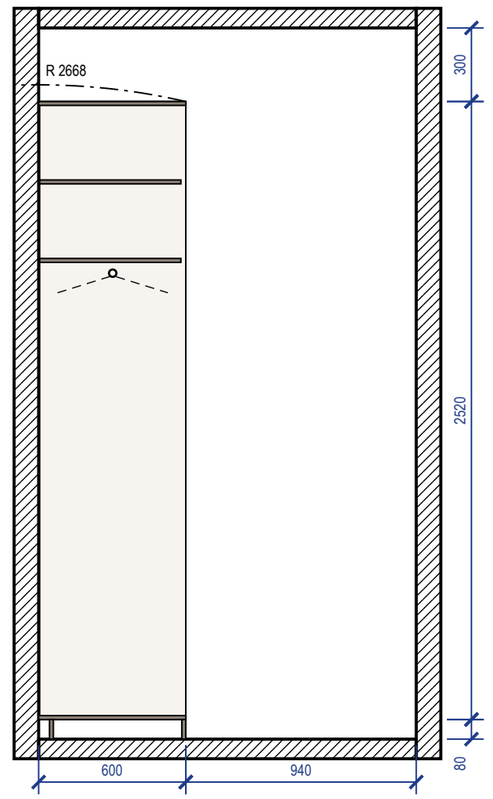



**Разрез 2-2**

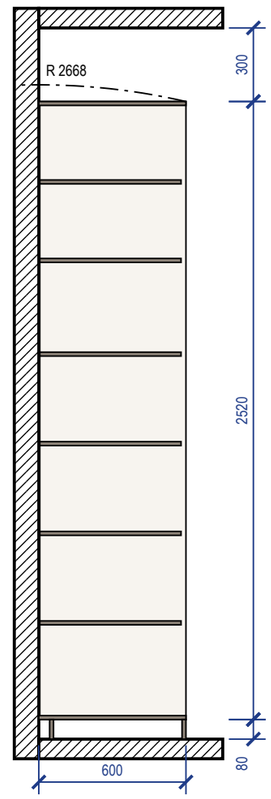


## Примечания

1. Размеры — в мм по чистовой отделке; изделие 1600×600×2600 (Ш×Г×В). Перед раскроем — контрольный замер цеха после чистовой отделки стен, пола и потолка.
2. Корпус — ЛДСП 16 мм, задняя стенка ХДФ 4 мм в паз, цоколь 80 мм на регулируемых опорах; открытая система без фасадов, ящики с фасадами.
3. Кромка: скрытые торцы 0,4 мм, видимые 2 мм (ПВХ/АБС).
4. Номинальные зазоры: между фасадами ящиков 3 мм, фасад ящика — стойка 2 мм.
5. Ящики — направляющие полного выдвижения NL 550 (внутренняя глубина 596 мм ≥ NL + 3); присадка по 32-й системе — выполняет цех.
6. Зазор до потолка 300 мм.
7. Подъём корпуса: диагональ боковины $\sqrt{(2600^2 + 600^2)} = 2668$ мм < 2900 мм до потолка — корпус собирается лёжа и поднимается поворотом.
8. Крепление к стене от опрокидывания: true; основание стены и шаг анкеров — монтажная схема шкафов.
9. Проход перед изделием 940 мм показан на разрезе 1-1.


**3D орто**

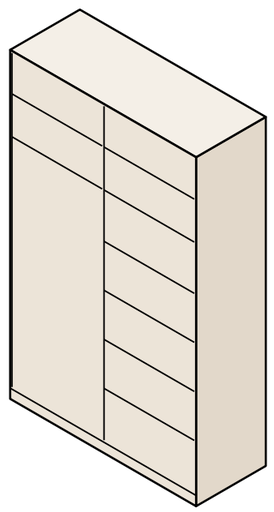


| | | | | | | |
|---|---|---|---|---|---|---|
| | | | | | Проект: Дом 120 м² | |
| | Лист | № док. | Подпись | Дата | | |
| Дизайнер | Кырлан А.С. | | | 19.10.26 | Система хранения M_38 | Стадия: П; Лист: Д_4; Листов: 104 |

выпуск 19.10.2026 № 46d0102a0d · стр. 94 из 104


**Общий вид**

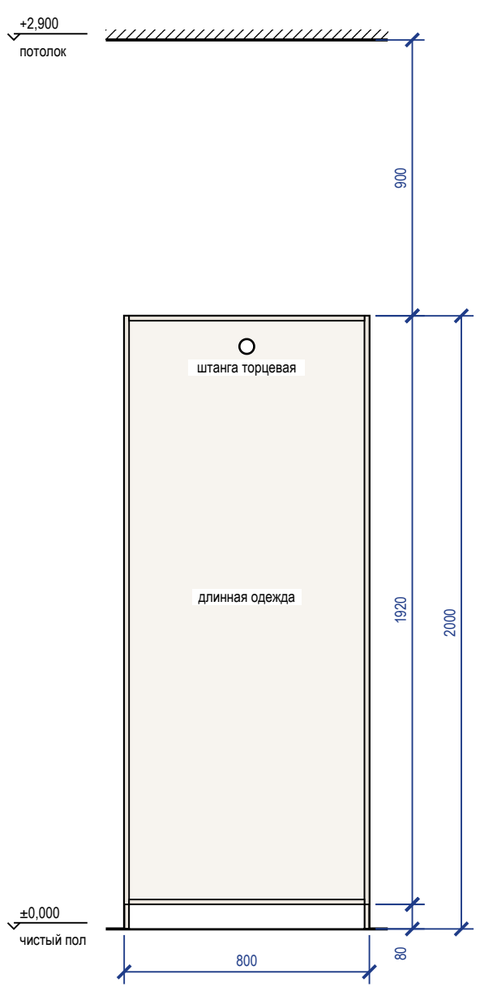


**Наполнение, размеры в свету**

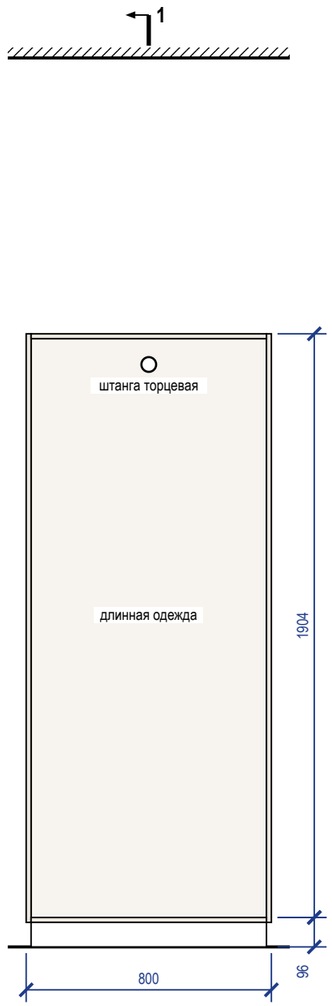



**Разрез 1-1**

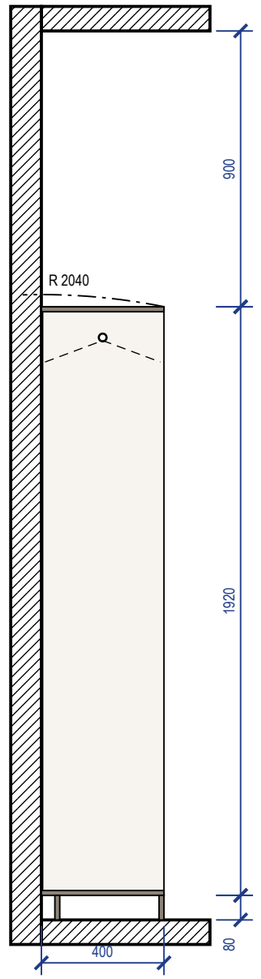


## Примечания

1. Размеры — в мм по чистовой отделке; изделие 800×400×2000 (Ш×Г×В). Перед раскроем — контрольный замер цеха после чистовой отделки стен, пола и потолка.
2. Корпус — ЛДСП 16 мм, задняя стенка ХДФ 4 мм в паз, цоколь 80 мм на регулируемых опорах; открытая система без фасадов, ящики с фасадами.
3. Кромка: скрытые торцы 0,4 мм, видимые 2 мм (ПВХ/АБС).
4. Номинальные зазоры: между фасадами ящиков 3 мм, фасад ящика — стойка 2 мм.
5. Ящики — направляющие полного выдвижения NL 350 (внутренняя глубина 396 мм ≥ NL + 3); присадка по 32-й системе — выполняет цех.
6. Зазор до потолка 900 мм.
7. Подъём корпуса: диагональ боковины $\sqrt{(2000^2 + 400^2)} = 2040$ мм < 2900 мм до потолка — корпус собирается лёжа и поднимается поворотом.
8. Крепление к стене от опрокидывания: true; основание стены и шаг анкеров — монтажная схема шкафов.


**3D орто**

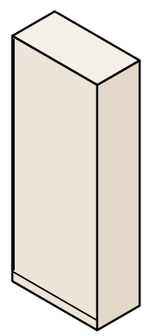


| | | | | | | | |
|---|---|---|---|---|---|---|---|
| | | | | | Проект: Дом 120 м² | | |
| | Лист | № док. | Подпись | Дата | Система хранения M_39 | Стадия | Лист | Листов |
| Дизайнер | Кырлан А.С. | | | 19.10.26 | | П | Д_5 | 104 |

выпуск 19.10.2026 № 46d0102a0d · стр. 95 из 104


## Общий вид

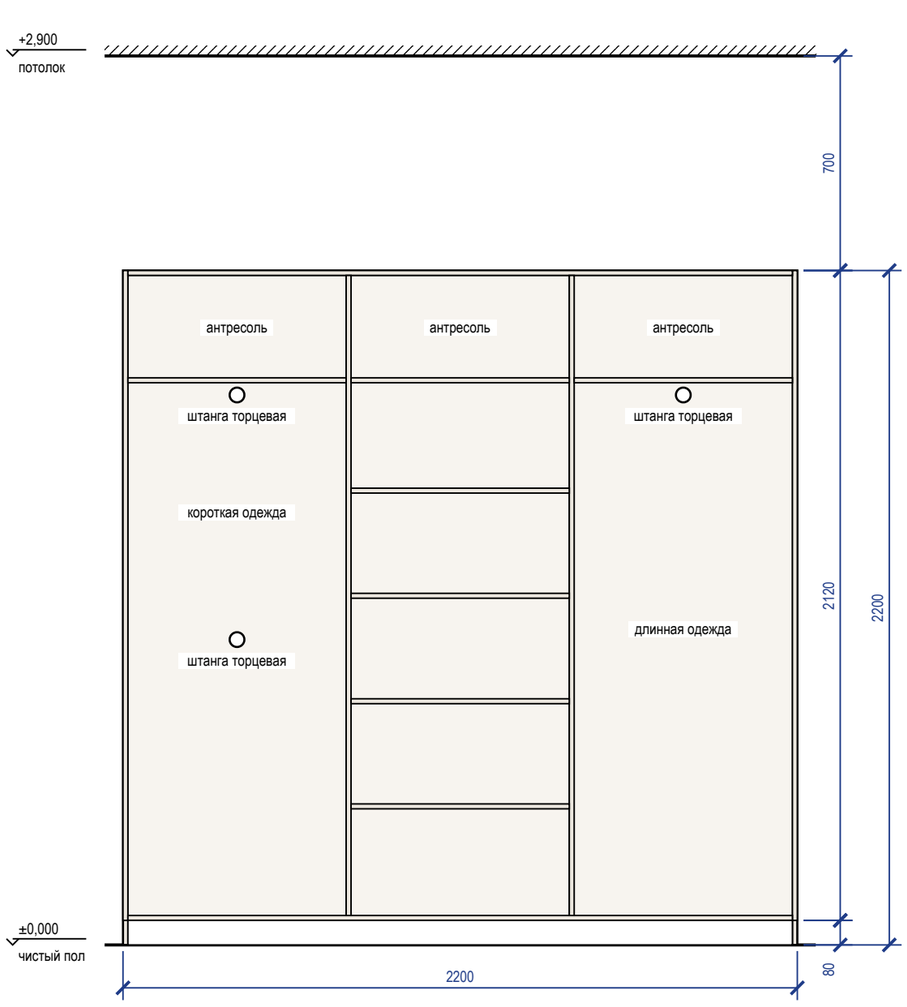



## Наполнение, размеры в свету

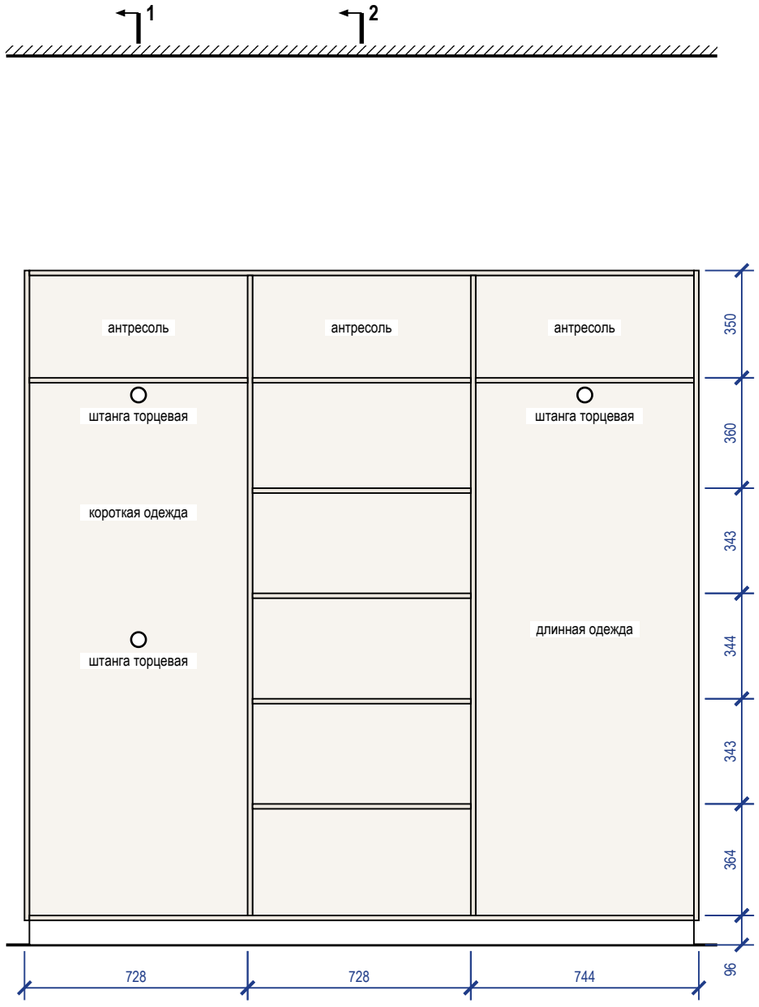


## Разрез 1-1

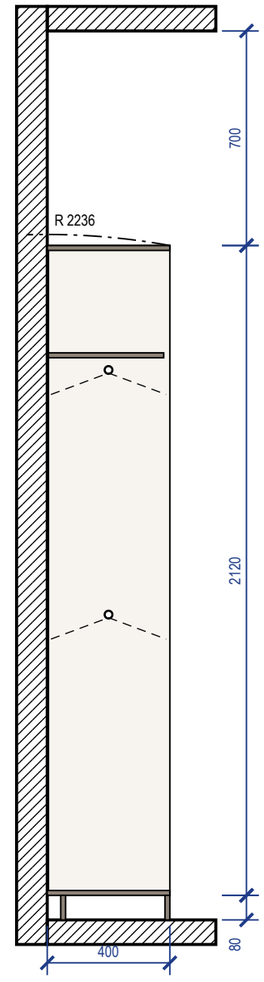



## Разрез 2-2

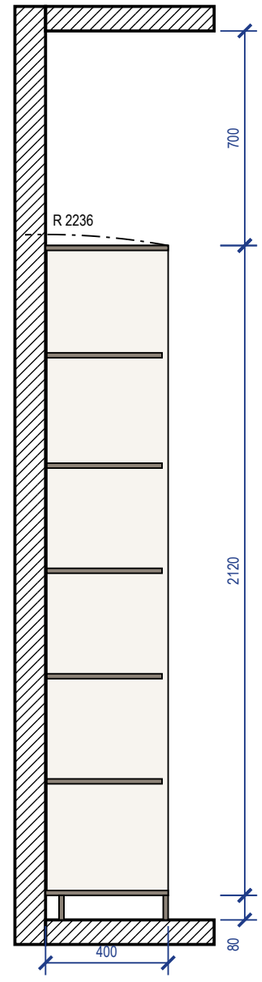


### Примечания

1. Размеры — в мм по чистовой отделке; изделие 2200×400×2200 (Ш×Г×В). Перед раскроем — контрольный замер цеха после чистовой отделки стен, пола и потолка.
2. Корпус — ЛДСП 16 мм, задняя стенка ХДФ 4 мм в паз, цоколь 80 мм на регулируемых опорах; открытая система без фасадов, ящики с фасадами.
3. Кромка: скрытые торцы 0,4 мм, видимые 2 мм (ПВХ/АБС).
4. Номинальные зазоры: между фасадами ящиков 3 мм, фасад ящика — стойка 2 мм.
5. Ящики — направляющие полного выдвижения NL 350 (внутренняя глубина 396 мм ≥ NL + 3); присадка по 32-й системе — выполняет цех.
6. Зазор до потолка 700 мм.
7. Подъём корпуса: диагональ боковины $\sqrt{(2200^2 + 400^2)} = 2236$ мм < 2900 мм до потолка — корпус собирается лёжа и поднимается поворотом.
8. Крепление к стене от опрокидывания: true; основание стены и шаг анкеров — монтажная схема шкафов.

## 3D орто

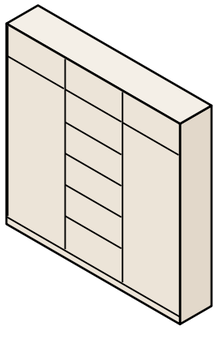


| | | | | | |
|---|---|---|---|---|---|
| | | | | | Проект: Дом 120 м² |
| | Лист | № док. | Подпись | Дата | Система хранения M_40 |
| Дизайнер | Кырлан А.С. | | | 19.10.26 | |


| Стадия | Лист | Листов |
|---|---|---|
| П | Д_6 | 104 |

выпуск 19.10.2026 № 46d0102a0d · стр. 96 из 104


## Общий вид

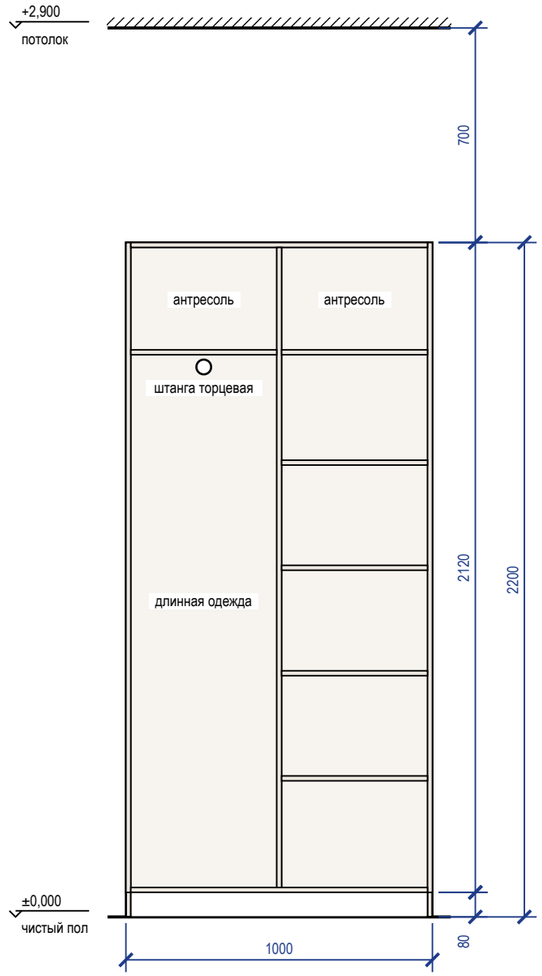



## Наполнение, размеры в свету

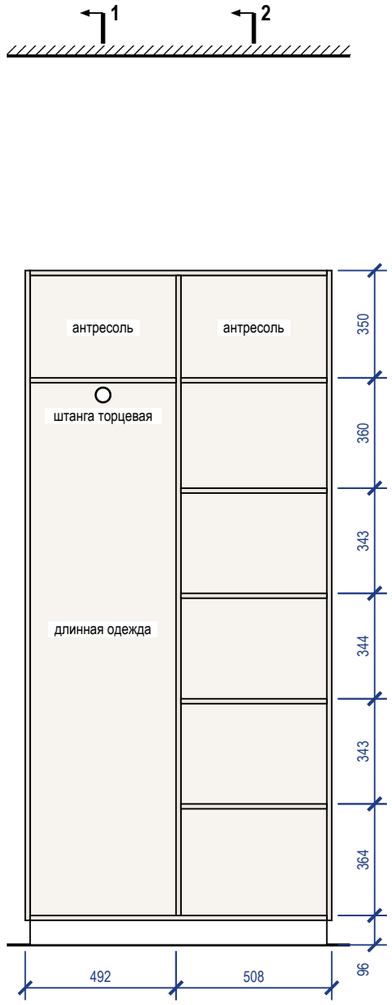


## Разрез 1-1

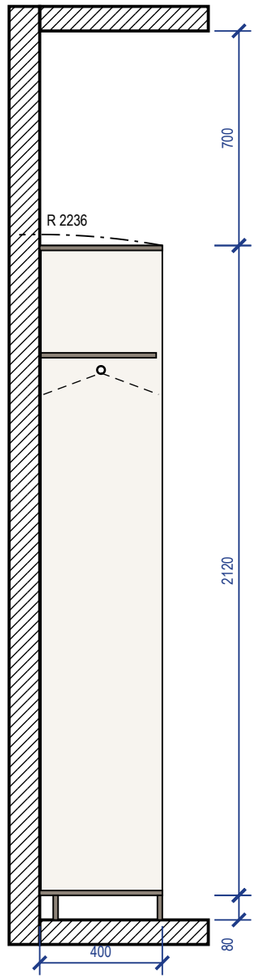



## Разрез 2-2

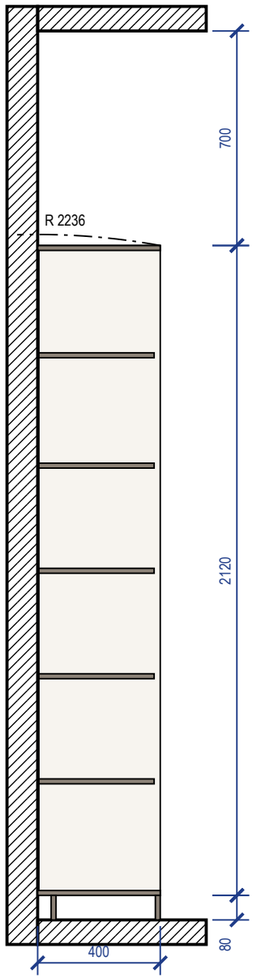


### Примечания

1. Размеры — в мм по чистовой отделке; изделие 1000×400×2200 (Ш×Г×В). Перед раскроем — контрольный замер цеха после чистовой отделки стен, пола и потолка.
2. Корпус — ЛДСП 16 мм, задняя стенка ХДФ 4 мм в паз, цоколь 80 мм на регулируемых опорах; открытая система без фасадов, ящики с фасадами.
3. Кромка: скрытые торцы 0,4 мм, видимые 2 мм (ПВХ/АБС).
4. Номинальные зазоры: между фасадами ящиков 3 мм, фасад ящика — стойка 2 мм.
5. Ящики — направляющие полного выдвижения NL 350 (внутренняя глубина 396 мм ≥ NL + 3); присадка по 32-й системе — выполняет цех.
6. Зазор до потолка 700 мм.
7. Подъём корпуса: диагональ боковины $\sqrt{(2200^2 + 400^2)} = 2236$ мм < 2900 мм до потолка — корпус собирается лёжа и поднимается поворотом.
8. Крепление к стене от опрокидывания: true; основание стены и шаг анкеров — монтажная схема шкафов.

## 3D орто

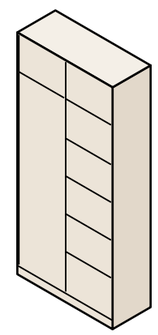


| | | | | | |
|---|---|---|---|---|---|
| | | | | | Проект: Дом 120 м² |
| | Лист | № док. | Подпись | Дата | Система хранения M_41 |
| Дизайнер | Кырлан А.С. | | | 19.10.26 | |


| Стадия | Лист | Листов |
|---|---|---|
| П | Д_7 | 104 |

выпуск 19.10.2026 № 46d0102a0d · стр. 97 из 104


## Вид с фасадами

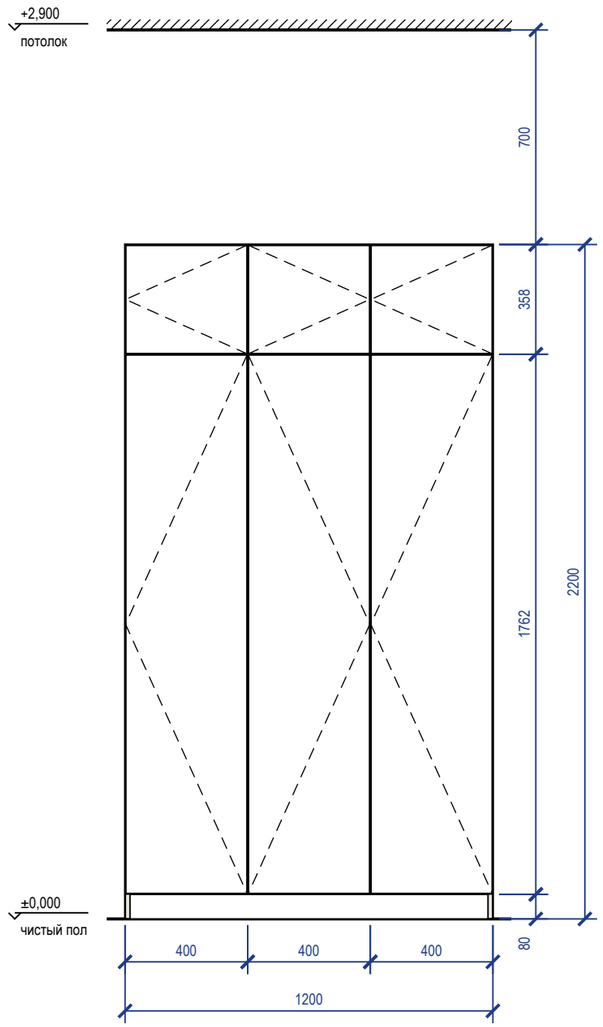



## Вид без фасадов

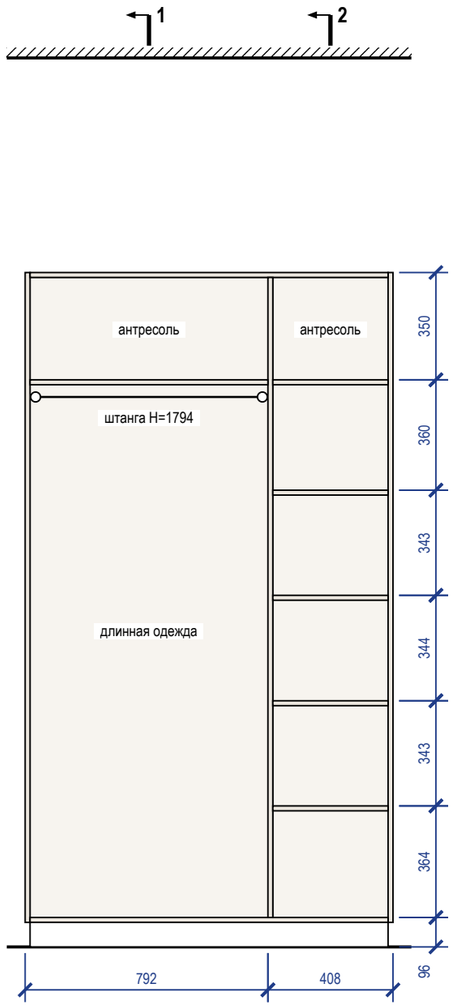


## Разрез 1-1

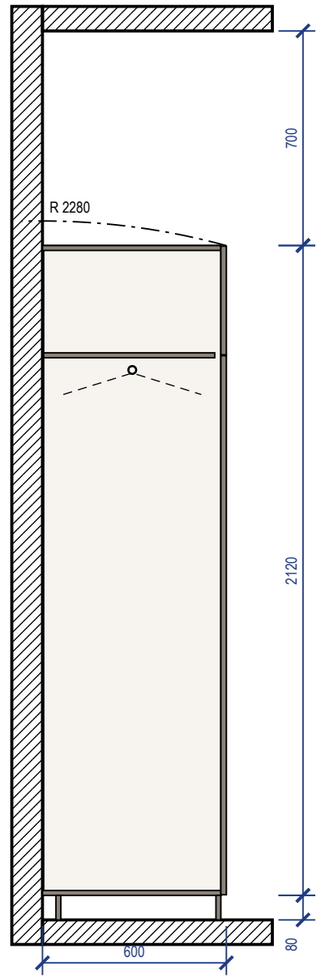



## Разрез 2-2

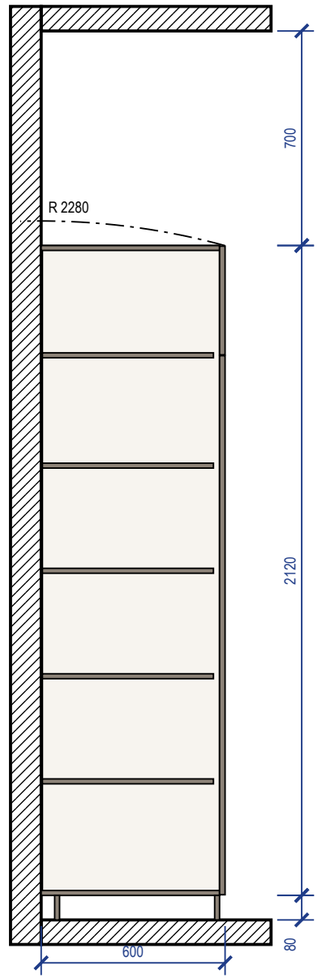


### Примечания

1. Размеры — в мм по чистовой отделке; изделие 1200×600×2200 (Ш×Г×В). Перед раскроем — контрольный замер цеха после чистовой отделки стен, пола и потолка.
2. Корпус — ЛДСП 16 мм, задняя стенка ХДФ 4 мм в паз, цоколь 80 мм на регулируемых опорах; фасады — МДФ, эмаль матовая 18 мм накладные, цвет — по колерной карте; петли с доводчиком: фасад 1759 мм — 4 петли, фасад 355 мм — 2 петли.
3. Кромка: скрытые торцы 0,4 мм, видимые 2 мм (ПВХ/АБС).
4. Номинальные зазоры: между фасадами 3 мм, фасад — стена и фасад — потолок не менее 3 мм, фасад ящика — стойка 2 мм.
5. Ящики — направляющие полного выдвижения NL 550 (внутренняя глубина 578 мм ≥ NL + 3); присадка по 32-й системе — выполняет цех.
6. Зазор до потолка 700 мм.
7. Подъём корпуса: диагональ боковины $\sqrt{(2200^2 + 600^2)} = 2280$ мм < 2900 мм до потолка — корпус собирается лёжа и поднимается поворотом.
8. Крепление к стене от опрокидывания — уголки 2 шт. к несущему основанию (монтажная схема шкафов).

## 3D орто

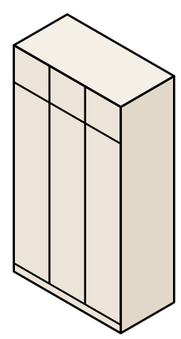


| | | | | | |
|---|---|---|---|---|---|
| | | | | | Проект: Дом 120 м² |
| | Лист | № док. | Подпись | Дата | |
| Дизайнер | Кырлан А.С. | | | 19.10.26 | Шкаф распашной М_45 |


| Стадия | Лист | Листов |
|---|---|---|
| П | Д_8 | 104 |

выпуск 19.10.2026 № 46d0102a0d · стр. 98 из 104


**Общий вид**

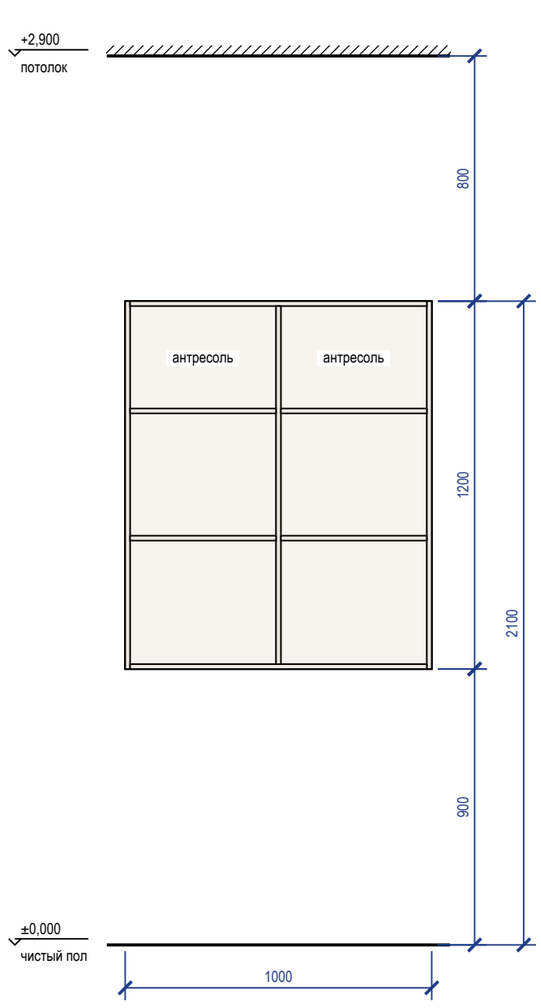


**Наполнение, размеры в свету**

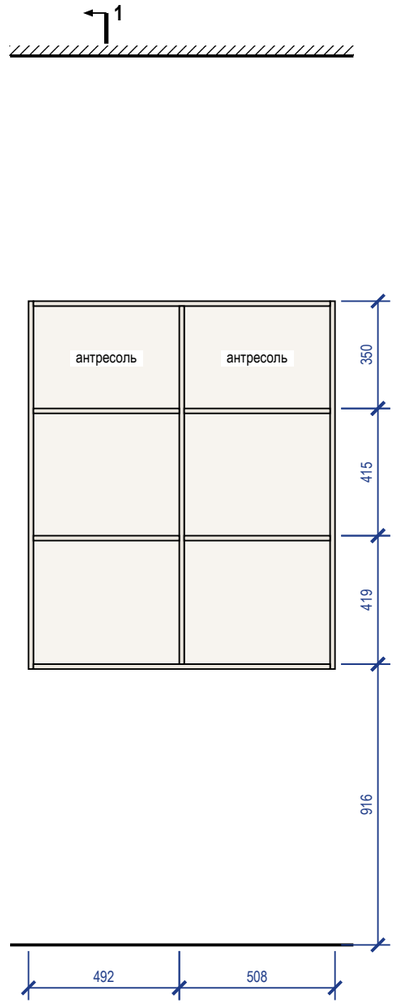



**Разрез 1-1**

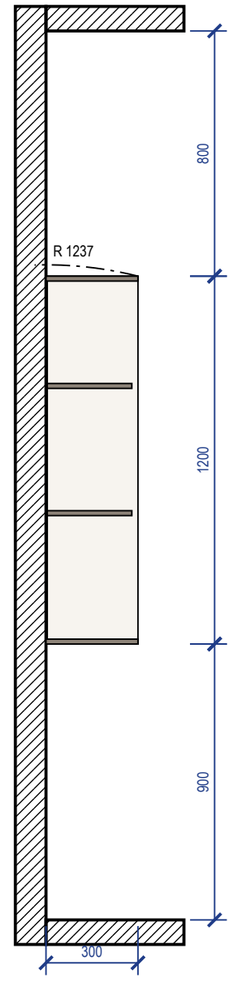


## Примечания

1. Размеры — в мм по чистовой отделке; изделие 1000×300×1200 (Ш×Г×В). Перед раскроем — контрольный замер цеха после чистовой отделки стен, пола и потолка.
2. Корпус — ЛДСП 16 мм, задняя стенка ХДФ 4 мм в паз, цоколь 0 мм на регулируемых опорах; открытая система без фасадов, ящики с фасадами.
3. Кромка: скрытые торцы 0,4 мм, видимые 2 мм (ПВХ/АБС).
4. Номинальные зазоры: между фасадами ящиков 3 мм, фасад ящика — стойка 2 мм.
5. Ящики — направляющие полного выдвижения NL 270 (внутренняя глубина 296 мм ≥ NL + 3); присадка по 32-й системе — выполняет цех.
6. Зазор до потолка 800 мм.
7. Подъём корпуса: диагональ боковины $\sqrt{(1200^2 + 300^2)} = 1237$ мм < 2000 мм до потолка — корпус собирается лёжа и поднимается поворотом.
8. Крепление к стене от опрокидывания: true; основание стены и шаг анкеров — монтажная схема шкафов.


**3D орто**

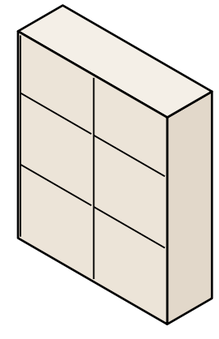


| | | | | | | |
|---|---|---|---|---|---|---|
| | | | | | Проект: Дом 120 м² | |
| | Лист | № док. | Подпись | Дата | | |
| Дизайнер | Кырлан А.С. | | | 19.10.26 | Система хранения M_47 | Стадия: П; Лист: Д_9; Листов: 104 |

выпуск 19.10.2026 № 46d0102a0d · стр. 99 из 104


## Вид с фасадами

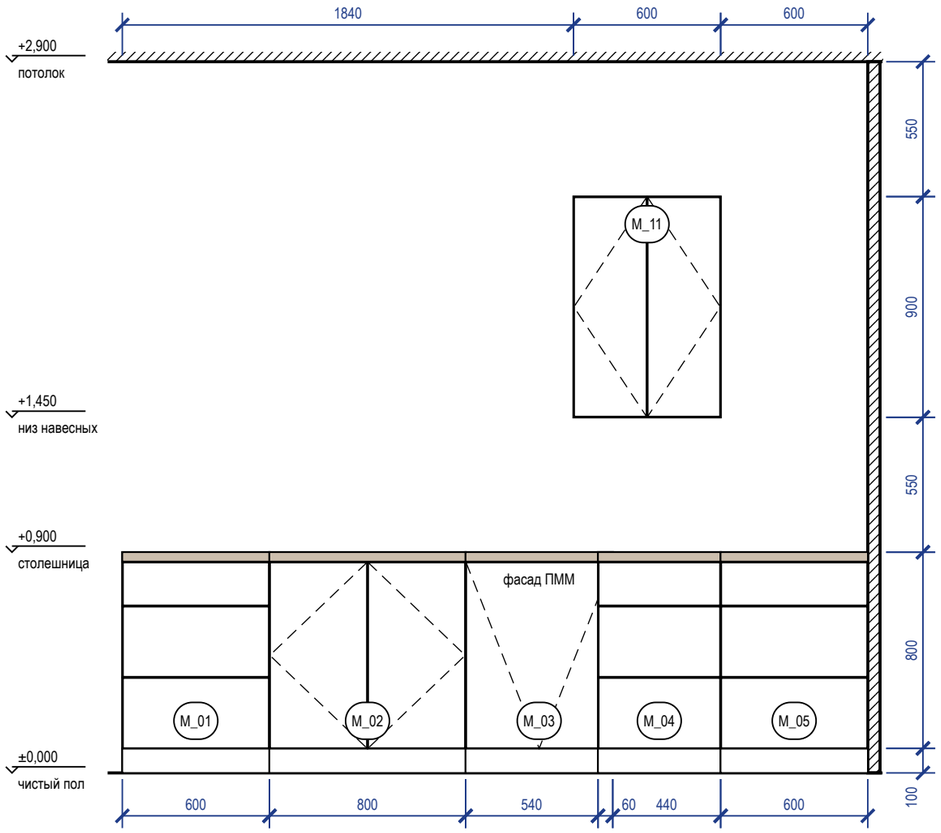



## Вид без фасадов (наполнение, выводы)

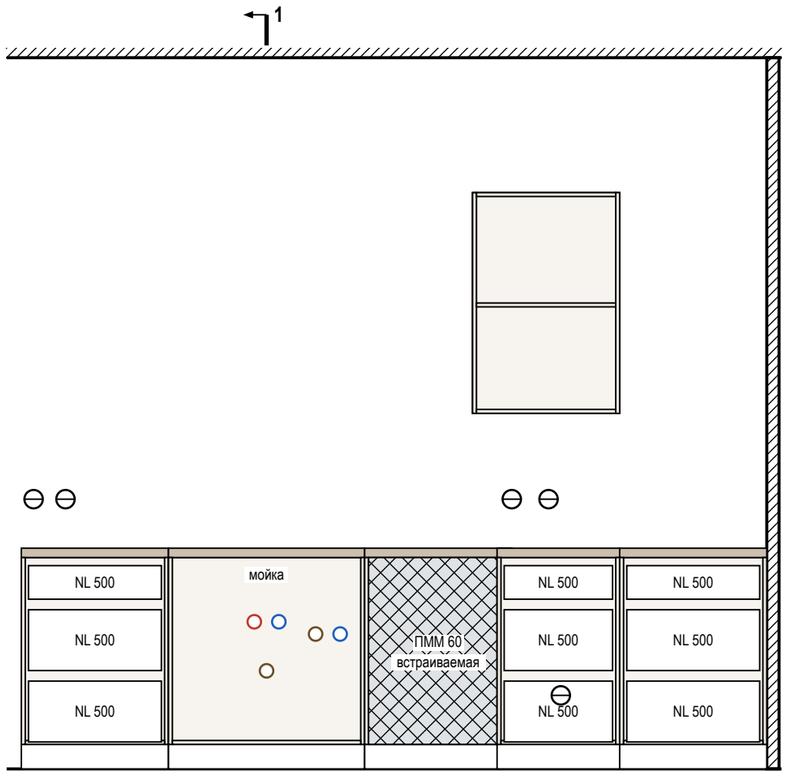


## Разрез 1-1

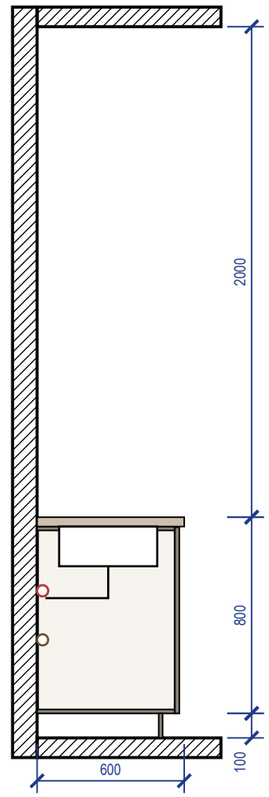


## 3D орто

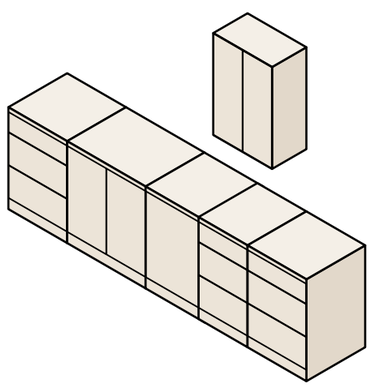

## Примечания


1. Размеры — в мм по чистовой отделке, вид из помещения; марки — как на плане расстановки. Перед раскроем — контрольный замер цеха после фартука и пола.
2. Корпуса — ЛДСП 16 мм, задняя стенка ХДФ 4 мм; фасады — МДФ, эмаль матовая 18 мм, цвет по колерной карте; столешница 38 мм, свес 20 мм; цоколь 100 мм.
3. Кромка: скрытые торцы 0,4 мм, видимые 2 мм. Номинальные зазоры: между фасадами 3 мм, фасад — столешница 3 мм, фасад — стена не менее 3 мм.
4. Ящики полного выдвижения и петли — с доводчиком; присадка по 32-й системе — выполняет цех.
5. Ниши техники — по монтажным схемам выбранных моделей: решётка в цоколе и канал за пеналом холодильника, зазор за духовым шкафом, фасад ПММ на двери машины.

| | | | | | |
|---|---|---|---|---|---|
| | | | | | Проект: Дом 120 м² |
| | Лист | № док. | Подпись | Дата | Кухня (пом. 1). Развёртка гарнитура |
| Дизайнер | Кырлан А.С. | | | 19.10.26 | |


| Стадия | Лист | Листов |
|---|---|---|
| П | Д_10 | 104 |

выпуск 19.10.2026 № 46d0102a0d · стр. 100 из 104


## Вид с фасадами

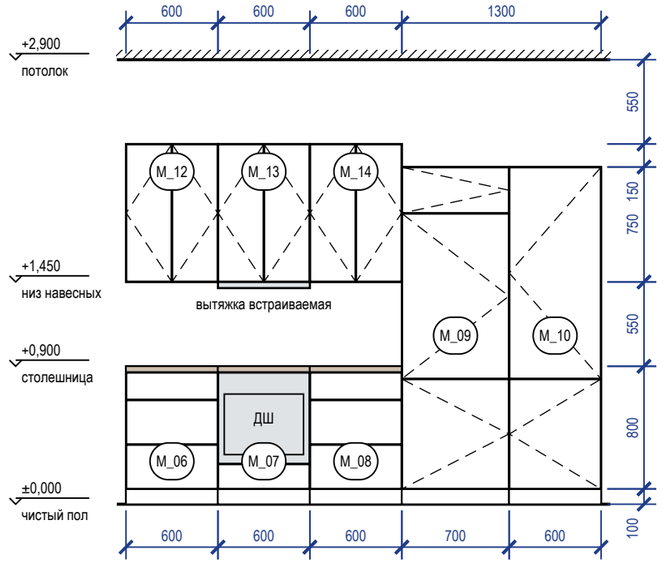



## Вид без фасадов (наполнение, выводы)

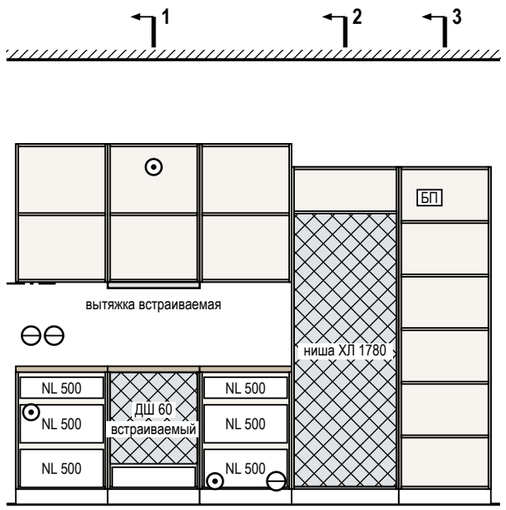



## Разрез 1-1

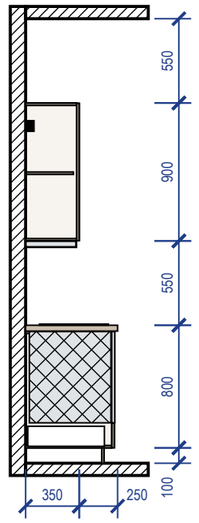



## Разрез 2-2

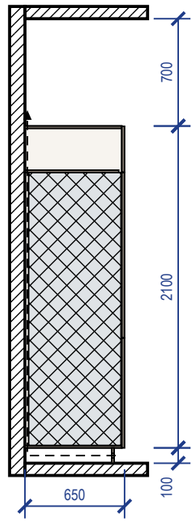


## Разрез 3-3

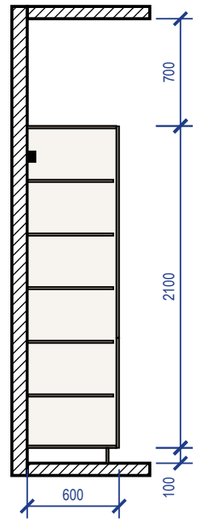


## 3D орто

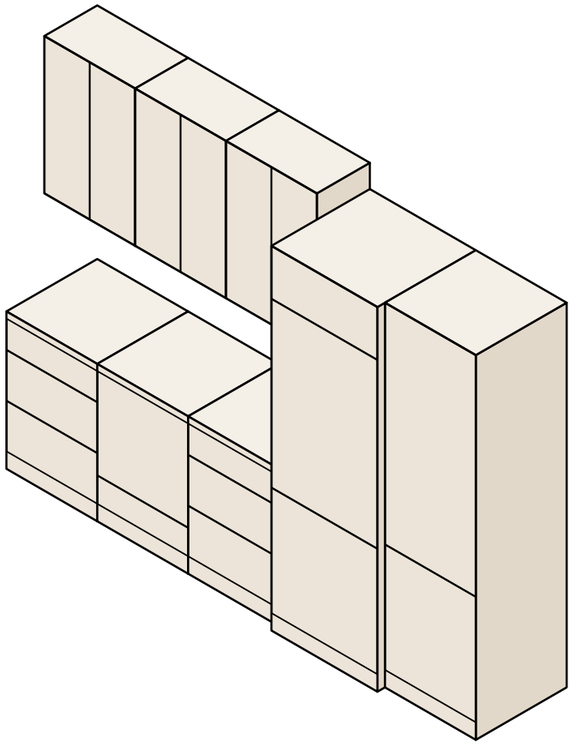

### Примечания

1. Размеры — в мм по чистовой отделке, вид из помещения; марки — как на плане расстановки. Перед раскроем — контрольный замер цеха после фартука и пола.
2. Корпуса — ЛДСП 16 мм, задняя стенка ХДФ 4 мм; фасады — МДФ, эмаль матовая 18 мм, цвет по колерной карте; столешница 38 мм, свес 20 мм; цоколь 100 мм.
3. Кромка: скрытые торцы 0,4 мм, видимые 2 мм. Номинальные зазоры: между фасадами 3 мм, фасад — столешница 3 мм, фасад — стена не менее 3 мм.
4. Ящики полного выдвижения и петли — с доводчиком; присадка по 32-й системе — выполняет цех.
5. Вытяжка встраивается в навесной модуль над варочной: её низ 510 мм над панелью — меньше 650 мм, модуль поднять или принять вытяжку с допуском по паспорту модели.
6. Ниши техники (холодильник — ориентир 1780 мм) — по монтажным схемам выбранных моделей: решётка в цоколе и канал за пеналом холодильника, зазор за духовым шкафом, фасад ПММ на двери машины.

| | | | | | |
|---|---|---|---|---|---|
| | | | | | Проект: Дом 120 м² |
| | Лист | № док. | Подпись | Дата | Кухня (пом. 1). Развёртка гарнитура |
| Дизайнер | Кырлан А.С. | | | 19.10.26 | |

| Стадия | Лист | Листов |
|---|---|---|
| П | Д_11 | 104 |

выпуск 19.10.2026 № 46d0102a0d · стр. 101 из 104

## Ведомость отделки помещений (форма 1 прил. А ГОСТ 21.501-2018). Лист 1 из 2

| № | Наименование помещения | Потолок | | | Стены и перегородки | | | Низ стен (плинтус) | | | Пол | | Примечание |
|---|---|---|---|---|---|---|---|---|---|---|---|---|---|
| | | Вид отделки | Код цвета | S, м² | Вид отделки | Код цвета | S, м² | Вид отделки | Код цвета | L, м | Вид отделки | S, м² | |
| 1 | Гостиная-кухня<br>31,32 м² | Окраска, Tikkurila Anti-Reflex 2, глубокоматовая, 2 слоя, подготовка Q3 | Little Greene No. 222 | 31,32 | Окраска, Farrow & Ball Modern Emulsion, матовая, 2 слоя, подготовка Q3<br>Акцент — стена А: окраска, Farrow & Ball Modern Emulsion, матовая, 2 слоя, подготовка Q3<br>Фартук кухни (стена А, Б): облицовка керамогранитом, аналог: керамогранит под травертин, матовый, 1200×600×9 мм, клей C2 TE S1, затирка CG2WA | Tikkurila G503<br>NCS S 3050-R80B<br>по артикулу | 43,15<br>11,58<br>2,00 | Плинтус МДФ h=80 мм, аналог: МДФ под покраску 80×16 | Tikkurila G503 | 21,7 | Инженерная доска, 1167-4250, 2100×127 мм, на клею; тип 1, отм. ЧП ±0,000 | 31,32 | Н стен 2900 (до потолка); матовая моющаяся, класс 1 EN 13300 — осознанно вместо полуматовой; плинтус в цвет: стены |
| 2 | Холл с лестницей<br>15,51 м² | Окраска, Tikkurila Anti-Reflex 2, глубокоматовая, 2 слоя, подготовка Q3 | Little Greene No. 222 | 15,51 | Окраска, Farrow & Ball Modern Emulsion, матовая, 2 слоя, подготовка Q3 | Tikkurila G503 | 34,65 | Плинтус МДФ h=80 мм, аналог: МДФ под покраску 80×16 | Tikkurila G503 | 11,1 | Инженерная доска, 1167-4250, 2100×127 мм, на клею; тип 1, отм. ЧП ±0,000 | 15,51 | Н стен 2900 (до потолка); матовая моющаяся, класс 1 EN 13300 — осознанно вместо полуматовой; плинтус в цвет: стены |
| 3 | Кабинет<br>11,00 м² | Окраска, Tikkurila Anti-Reflex 2, глубокоматовая, 2 слоя, подготовка Q3 | Little Greene No. 222 | 11,00 | Окраска, Farrow & Ball Modern Emulsion, матовая, 2 слоя, подготовка Q3<br>Акцент — стена А: окраска, Farrow & Ball Modern Emulsion, матовая, 2 слоя, подготовка Q3 | Tikkurila G503<br>NCS S 5020-G90Y | 23,97<br>10,85 | Плинтус МДФ h=80 мм, аналог: МДФ под покраску 80×16 | Tikkurila G503 | 12,6 | Инженерная доска, 1167-4250, 2100×127 мм, на клею; тип 1, отм. ЧП ±0,000 | 11,00 | Н стен 2900 (до потолка); плинтус в цвет: стены |
| 4 | Санузел гостевой<br>4,17 м² | Окраска, Tikkurila Luja 7, матовая, 2 слоя, подготовка Q3 | Little Greene No. 222 | 4,17 | Облицовка плиткой, A8UZ, 600×1200×9 мм, клей C2 TE S1, затирка CG2WA | Atlas Concorde A8UZ | 17,40 | нет | | | Керамогранит, A8UZ, 600×1200×9 мм; тип 2, отм. ЧП −0,015 | 4,17 | Н стен 2915 (до потолка); гидроизоляция обмазочная, 2 слоя, с заведением на стены 200 мм (по пирогу пола); тест проливом и акт скрытых работ |
| 5 | Прихожая<br>12,20 м² | Окраска, Tikkurila Anti-Reflex 2, глубокоматовая, 2 слоя, подготовка Q3 | Little Greene No. 222 | 12,20 | Окраска, Farrow & Ball Modern Emulsion, матовая, 2 слоя, подготовка Q3 | Tikkurila G503 | 43,20 | Плинтус МДФ h=80 мм, аналог: МДФ под покраску 80×16 | Tikkurila G503 | 14,0 | Керамогранит, A8UZ, 600×1200×9 мм; тип 3, отм. ЧП ±0,000 | 12,20 | Н стен 2900 (до потолка); матовая моющаяся, класс 1 EN 13300 — осознанно вместо полуматовой; плинтус в цвет: стены |
| 6 | Спальня родителей<br>17,17 м² | Окраска, Tikkurila Anti-Reflex 2, глубокоматовая, 2 слоя, подготовка Q3 | Little Greene No. 222 | 17,17 | Окраска, Farrow & Ball Modern Emulsion, матовая, 2 слоя, подготовка Q3<br>Акцент — стена А: окраска, Farrow & Ball Modern Emulsion, матовая, 2 слоя, подготовка Q3 | Tikkurila G503<br>Farrow & Ball No. 89 | 35,79<br>8,15 | Плинтус МДФ h=80 мм, аналог: МДФ под покраску 80×16 | Tikkurila G503 | 15,9 | Инженерная доска, 1167-4250, 2100×127 мм, на клею; тип 1, отм. ЧП ±0,000 | 17,17 | Н стен 2900 (до потолка); плинтус в цвет: стены |
| 7 | Детская<br>12,30 м² | Окраска, Tikkurila Anti-Reflex 2, глубокоматовая, 2 слоя, подготовка Q3 | Little Greene No. 222 | 12,30 | Окраска, Farrow & Ball Modern Emulsion, матовая, 2 слоя, подготовка Q3<br>Акцент — стена А: окраска, Farrow & Ball Modern Emulsion, матовая, 2 слоя, подготовка Q3 | Tikkurila G503<br>Farrow & Ball No. 66 | 26,07<br>10,85 | Плинтус МДФ h=69 мм, SX165 | Tikkurila G503 | 13,3 | Инженерная доска, 1167-4250, 2100×127 мм, на клею; тип 1, отм. ЧП ±0,000 | 12,30 | Н стен 2900 (до потолка); плинтус в цвет: стены |
| 8 | Гардеробная<br>3,82 м² | Окраска, Tikkurila Anti-Reflex 2, глубокоматовая, 2 слоя, подготовка Q3 | Little Greene No. 222 | 3,82 | Окраска, Tikkurila Harmony, матовая, 2 слоя, подготовка Q3 | Little Greene No. 222 | 22,06 | Плинтус МДФ h=80 мм, аналог: МДФ под покраску 80×16 | Little Greene No. 222 | 7,4 | Инженерная доска, 1167-4250, 2100×127 мм, на клею; тип 1, отм. ЧП ±0,000 | 3,82 | Н стен 2900 (до потолка); плинтус в цвет: стены |
| 9 | Кладовая<br>4,66 м² | Окраска, Tikkurila, глубокоматовая | NCS S 0300-N | 4,66 | Окраска, Tikkurila, матовая, подготовка Q3 | NCS S 0502-Y | 23,61 | Плинтус МДФ h=69 мм, SX165 | NCS S 0300-N | 7,9 | Инженерная доска, 1167-4250, 2100×127 мм, на клею; тип 4, отм. ЧП ±0,000 | 4,66 | Н стен 2900 (до потолка) |
| 10 | Холл второго этажа<br>15,51 м² | Окраска, Tikkurila Anti-Reflex 2, глубокоматовая, 2 слоя, подготовка Q3 | Little Greene No. 222 | 15,51 | Окраска, Farrow & Ball Modern Emulsion, матовая, 2 слоя, подготовка Q3 | Tikkurila G503 | 34,65 | Плинтус МДФ h=80 мм, аналог: МДФ под покраску 80×16 | Tikkurila G503 | 11,1 | Инженерная доска, 1167-4250, 2100×127 мм, на клею; тип 1, отм. ЧП ±0,000 | 15,51 | Н стен 2900 (до потолка); матовая моющаяся, класс 1 EN 13300 — осознанно вместо полуматовой; плинтус в цвет: стены |

### Примечания

1. Ведомость продолжена на листе 2 из 2; итоги, сводка площадей и примечания — на последнем листе ведомости.

| | | | | | |
|---|---|---|---|---|---|
| | | | | | Проект: Дом 120 м² |
| | Лист | № док. | Подпись | Дата | Ведомость отделки помещений. Лист 1 из 2 |
| Дизайнер | Кырлан А.С. | | | 19.10.26 | |

| Стадия | Лист | Листов |
|---|---|---|
| П | С1 | 104 |

выпуск 19.10.2026 № 46d0102a0d · стр. 102 из 104


| Поз. | Наименование и техническая характеристика | Тип, марка, обозначение документа | Код продукции | Поставщик | Ед. изм. | Кол. | Образец | Примечание |
|---|---|---|---|---|---|---|---|---|
| | **Лакокрасочные материалы** | | | | | | | |
| 1 | Краска интерьерная водно-дисперсионная акриловая для стен, матовая, класс мокрого истирания 1 по EN 13300, база A; цвет Tikkurila G503 «Calla», колеровка машинная | Farrow & Ball Modern Emulsion | | Farrow & Ball | л | 77,5 | | поз. К1 колерной карты; пом. 1, 2, 3, 5, 6, 7, 10, 11, 12; S = 284,9 м² × 2 сл. × 0,12 л/м² = 68,4 л, +10 % и 0,5 л на подкраску → ≥ 75,7 л; тара 15 × 5 л + 1 × 2,5 л |
| 2 | Краска интерьерная водно-дисперсионная акриловая для акцентных стен, матовая, класс мокрого истирания 1 по EN 13300, база C; цвет NCS S 3050-R80B «Эгейский синий», колеровка машинная | Farrow & Ball Modern Emulsion | | Farrow & Ball | л | 5 | | поз. К2 колерной карты; пом. 1; S = 11,6 м² × 2 сл. × 0,12 л/м² = 2,8 л, +10 % и 0,5 л на подкраску → ≥ 3,6 л; тара 1 × 5 л |
| 3 | Краска интерьерная водно-дисперсионная акриловая для потолков, глубокоматовая, класс мокрого истирания 2 по EN 13300, база A; цвет Little Greene No. 222 «Loft White», колеровка машинная | Tikkurila Anti-Reflex 2 | | Tikkurila | л | 36 | | поз. К3 колерной карты; пом. 1, 2, 3, 5, 6, 7, 8, 10, 11, 12; S = 133,2 м² × 2 сл. × 0,12 л/м² = 32,0 л, +10 % и 0,5 л на подкраску → ≥ 35,7 л; тара 4 × 9 л |
| 4 | Краска интерьерная водно-дисперсионная акриловая для акцентных стен, матовая, класс мокрого истирания 1 по EN 13300, база C; цвет NCS S 5020-G90Y «Олива», колеровка машинная | Farrow & Ball Modern Emulsion | | Farrow & Ball | л | 5 | | поз. К5 колерной карты; пом. 3; S = 10,8 м² × 2 сл. × 0,12 л/м² = 2,6 л, +10 % и 0,5 л на подкраску → ≥ 3,4 л; тара 1 × 5 л |
| 5 | Краска интерьерная водно-дисперсионная акриловая для потолков, матовая, класс мокрого истирания 1 по EN 13300, база A; цвет Little Greene No. 222 «Loft White», колеровка машинная | Tikkurila Luja 7 | | Tikkurila | л | 3,6 | | поз. К7 колерной карты; пом. 4, 13; S = 9,5 м² × 2 сл. × 0,12 л/м² = 2,3 л, +10 % и 0,5 л на подкраску → ≥ 3,0 л; тара 1 × 2,7 л + 1 × 0,9 л |
| 6 | Краска интерьерная водно-дисперсионная акриловая для акцентных стен, матовая, класс мокрого истирания 1 по EN 13300, база C; цвет Farrow & Ball No. 89 «Lulworth Blue — светлая морская лазурь», колеровка машинная | Farrow & Ball Modern Emulsion | | Farrow & Ball | л | 5 | | поз. К8 колерной карты; пом. 6; S = 8,1 м² × 2 сл. × 0,12 л/м² = 2,0 л, +10 % и 0,5 л на подкраску → ≥ 2,7 л; тара 1 × 5 л |
| 7 | Краска интерьерная водно-дисперсионная акриловая для акцентных стен, матовая, класс мокрого истирания 1 по EN 13300, база C; цвет Farrow & Ball No. 66 «India Yellow — охра / горчица итальянских фасадов», колеровка машинная | Farrow & Ball Modern Emulsion | | Farrow & Ball | л | 5 | | поз. К9 колерной карты; пом. 7; S = 10,8 м² × 2 сл. × 0,12 л/м² = 2,6 л, +10 % и 0,5 л на подкраску → ≥ 3,4 л; тара 1 × 5 л |
| 8 | Краска интерьерная водно-дисперсионная акриловая для стен, матовая, класс мокрого истирания 1 по EN 13300, база A; цвет Little Greene No. 222 «Loft White», колеровка машинная | Tikkurila Harmony | | Tikkurila | л | 7,2 | | поз. К11 колерной карты; пом. 8; S = 22,1 м² × 2 сл. × 0,12 л/м² = 5,3 л, +10 % и 0,5 л на подкраску → ≥ 6,3 л; тара 2 × 2,7 л + 2 × 0,9 л |
| 9 | Краска интерьерная водно-дисперсионная акриловая для стен, матовая, класс мокрого истирания 2 по EN 13300, база A; цвет NCS S 0502-Y, колеровка машинная | Tikkurila | | Tikkurila | л | 7,2 | | поз. К13 колерной карты; пом. 9; S = 23,6 м² × 2 сл. × 0,12 л/м² = 5,7 л, +10 % и 0,5 л на подкраску → ≥ 6,7 л; тара 2 × 2,7 л + 2 × 0,9 л |
| 10 | Краска интерьерная водно-дисперсионная для потолков, глубокоматовая, класс мокрого истирания 2 по EN 13300, база A; цвет NCS S 0300-N, колеровка машинная | Tikkurila | | Tikkurila | л | 1,8 | | поз. К14 колерной карты; пом. 9; S = 4,7 м² × 2 сл. × 0,12 л/м² = 1,1 л, +10 % и 0,5 л на подкраску → ≥ 1,7 л; тара 2 × 0,9 л |
| 11 | Краска интерьерная водно-дисперсионная акриловая для акцентных стен, матовая, класс мокрого истирания 1 по EN 13300, база C; цвет Tikkurila H440 «H440 Wave — бирюзово-голубая вода», колеровка машинная | Farrow & Ball Modern Emulsion | | Farrow & Ball | л | 2,5 | | поз. К16 колерной карты; пом. 12; S = 7,4 м² × 2 сл. × 0,12 л/м² = 1,8 л, +10 % и 0,5 л на подкраску → ≥ 2,5 л; тара 1 × 2,5 л |
| 12 | Краска для МДФ и дерева в цвет Tikkurila G503 «Calla» — окраска плинтуса; блеск не ниже блеска стен | марка не задана | | | л | 2,9 | | поз. К4, К10; пом. 1, 2, 3, 5, 6, 7, 10, 11, 12; L = 116,5 м, S = 10,9 м² × 2 сл. × 0,12 л/м² + 10 %; продукт подобрать в веере Tikkurila |
| 13 | Краска для МДФ и дерева в цвет Little Greene No. 222 «Loft White» — окраска плинтуса; блеск не ниже блеска стен | марка не задана | | | л | 0,5 | | поз. К12; пом. 8; L = 7,4 м, S = 0,7 м² × 2 сл. × 0,12 л/м² + 10 %; продукт подобрать в веере Little Greene |
| 14 | Акрил, полуматовая в цвет NCS S 0300-N — окраска плинтуса | аналог по характеристикам | | | л | 0,5 | | поз. К15; пом. 9; L = 7,9 м, S = 0,7 м² × 2 сл. × 0,12 л/м² + 10 %; продукт подобрать в веере NCS |
| 15 | Грунтовка акриловая под окраску стен и потолков — из системы производителя краски | по системе краски | | | м² | 527 | | площадь окраски стен, акцентов и потолков; 1 слой перед окраской; расход — по ТУ грунтовки |

| | | | | | |
|---|---|---|---|---|---|
| | | | | | Проект: Дом 120 м² |
| | Лист | № док. | Подпись | Дата | Спецификация отделочных материалов |
| Дизайнер | Кырлан А.С. | | | 19.10.26 | |

| Стадия | Лист | Листов |
|---|---|---|
| П | С2 | 104 |


## 1 Порог 15 мм: мокрая зона — жилое помещение (М 1:5)

Применение: двери Д-3, Д-8

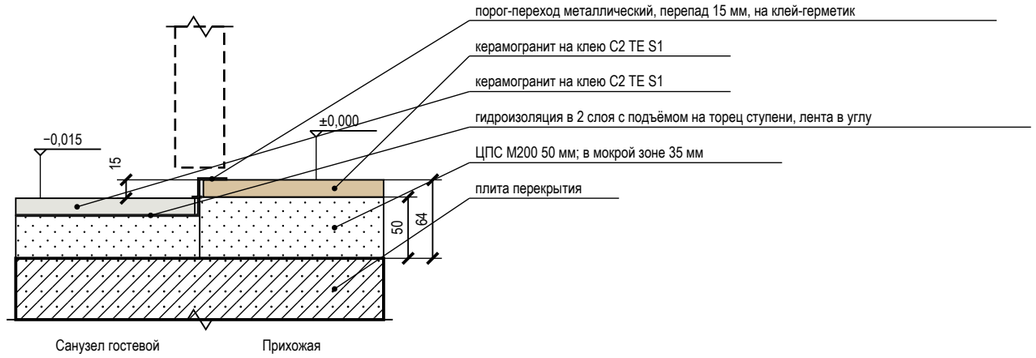



## 2 Дверь скрытого монтажа в плоскости стены, плинтус (М 1:5)

Применение: двери Д-1, Д-2, Д-3, Д-4, Д-5, Д-6, Д-7, Д-10, Д-9, Д-8

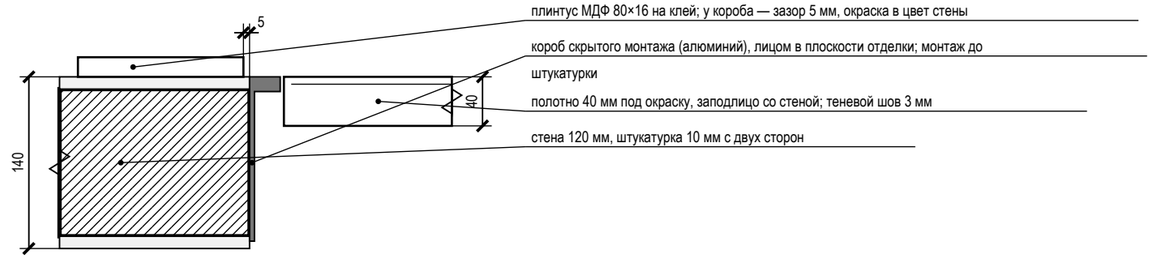



## 3 Короб стояков К1-1 с люком и звукоизоляцией (М 1:10)

Применение: пом. 4, 1

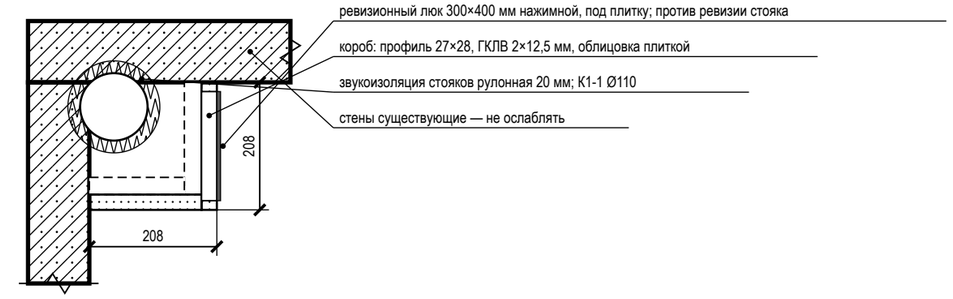



## 4 Гидроизоляция санузла: заход на стены 200 мм, примыкание ванны (М 1:20)

Применение: пом. 4, 13

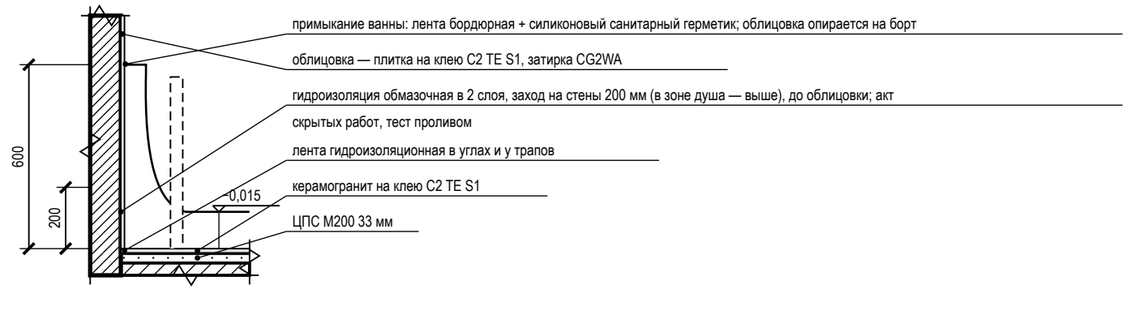


## 5 Плинтус МДФ 80×16 мм у окрашенной стены (М 1:10)

Применение: пом. 1, 2, 3, 5, 6, 7, 8, 9, 10, 11, 12

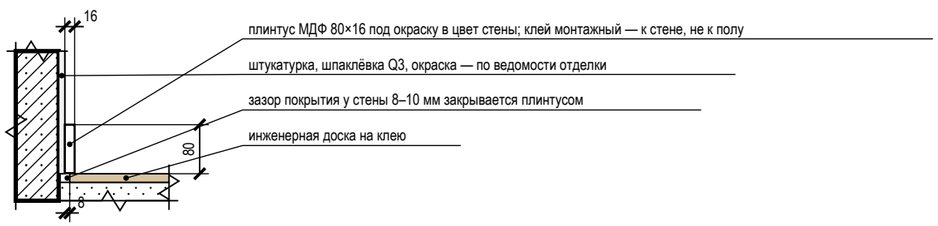


## Условные обозначения

- железобетон (плита, стены)
- кладка, перегородка
- стяжка, раствор
- гипсокартон ГКЛВ
- звукоизоляция, эластичный заполнитель
- плитка, керамогранит на клею
- инженерная доска (покрытие пола)
- металлический профиль (порог, Т-профиль, короб двери)
- гидроизоляция (обмазочная, лента)

## Примечания

1. Узлы — типовые решения проекта для мест, отмеченных выносками на листе схемы расположения развёрток и узлов; размеры — в мм, отметки — в м от ±0,000.
2. Узлы с гидроизоляцией, закладными и коробами скрытого монтажа принимаются по актам скрытых работ до закрытия отделкой; гидроизоляция — после теста проливом (24 ч).
3. Марки изделий (порог, Т-профиль, короб скрытой двери, люк) — по спецификациям; замена — на аналог с теми же габаритами по согласованию с автором проекта.

| | | | | | |
|---|---|---|---|---|---|
| | | | | | Проект: Дом 120 м² |
| | Лист | № док. | Подпись | Дата | |
| Дизайнер | Кырлан А.С. | | | 19.10.26 | Узлы |

| Стадия | Лист | Листов |
|---|---|---|
| П | С3 | 104 |

выпуск 19.10.2026 № 46d0102a0d · стр. 104 из 104