ДИЗАЙН-ПРОЕКТ ИНТЕРЬЕРА

Дом 331 м²

Шале

270,67 м²

защищённый · тёплый · основательный · природный · камерный · после мороза — у огня

Современное шале 60 % + эко (eco-organic.json) 40 %: загородный дом у леса. Стены — шерстяной белый Joa's White No. 226 и молочный S 0804-Y30R, потолки — известковый Slaked Lime No. 105; второй план — выцветший оливковый V451, шалфей S 3020-G30Y, песчаник X463; акценты — хвойный S 7020-G10Y, терракота Red Earth No. 64, брусника Eating Room Red No. 43. Дерево — дуб и лиственница под маслом, камень у камина.

ПАЛИТРА 60 / 30 / 10

F&B No. 226	NCS S 0804-Y30R	Little Greene No. 105	V451	NCS S 3020-G30Y
60 %	60 %	60 %	30 %	30 %



Визуализация 1 · Вид сверху (3D): планировка с мебелью, текстилем и декором

ОБЪЕКТ	ОБЩАЯ ПЛОЩАДЬ	ПОМЕЩЕНИЙ
Дом 331 м²	270,67 м²	20, из них жилых 6
СТИЛЬ	**СТАДИЯ**	**ШИФР**
Шале	Рабочий проект	ГД-2026-010-АИ

АВТОР ПРОЕКТА

Кырлан Александр Сергеевич

Октябрь 2026

					Проект: Дом 331 м²			
	Лист	№ док.	Подпись	Дата	Титульный лист	Стадия	Лист	Листов
Дизайнер	Кырлан А.С.			19.10.26		П	1	155

выпуск 18.10.2026 · ffc1f29499 · стр. 1 из 155

Список листов

Лист	Наименование
1	Титульный лист
2	Список листов
3	План планировки от заказчика · 1-й этаж
4	План планировки от заказчика · Мансарда
5	План монтажный · 1-й этаж
6	План монтажный · Мансарда
7	Кухня (пом. 1). Монтажная схема
8	Шкафы. Монтажная схема. Лист 1 из 2
9	Шкафы. Монтажная схема. Лист 2 из 2
10	Карта покрытий стен · 1-й этаж
11	Карта покрытий стен · Мансарда
12	Колерная карта
13	План размещения мебели и оборудования · 1-й этаж
14	План размещения мебели и оборудования · Мансарда
15	Спецификация мебели и оборудования
16	Спецификация мебели и оборудования (продолжение)
17	Спецификация мебели и оборудования (продолжение)
18	Спецификация мебели и оборудования (продолжение)
19	Ведомости изделий, техники и фурнитуры
20	План выводов сантехники · 1-й этаж
21	План выводов сантехники · Мансарда
22	Схема разводки водопровода и канализации · 1-й этаж
23	Схема разводки водопровода и канализации · Мансарда
24	Спецификация сантехнического оборудования
25	Раскладка плитки. Санузел 1 этажа. Развёртки стен
26	Раскладка плитки. Санузел мастер. Развёртки стен
27	Раскладка плитки. Санузел 2. Развёртки стен
28	План размещения дверей · 1-й этаж
29	План размещения дверей · Мансарда
30	Лестница Л-1
31	План потолков · 1-й этаж
32	План потолков · Мансарда
33	План розеток и электровыводов · 1-й этаж
34	План розеток и электровыводов · Мансарда
35	План слаботочных сетей · 1-й этаж
36	План слаботочных сетей · Мансарда
37	План освещения · 1-й этаж
38	План освещения · Мансарда
39	Спецификация светильников и сценарии освещения
40	Управление светильниками · 1-й этаж
41	Управление светильниками · Мансарда
42	План вентиляции · 1-й этаж
43	План вентиляции · Мансарда
44	План отопления · 1-й этаж
45	План отопления · Мансарда
46	План покрытий пола · 1-й этаж
47	План покрытий пола · Мансарда
48	Раскладка плитки. Планы полов
49	Раскладка плитки. Котельная. Прихожая. Тамбур. Веранда
50	Визуализация. Вид сверху
51	Визуализация. Вид сверху
52	Визуализация: Кухня-столовая
53	Визуализация: Кухня-столовая
54	Развёртка стены А. Кухня-столовая (пом. 1), кухонный фронт
55	Развёртка стены Б. Кухня-столовая (пом. 1)
56	Развёртка стены В. Кухня-столовая (пом. 1)
57	Развёртка стены Г. Кухня-столовая (пом. 1)
58	Визуализация: Кабинет-гостевая
59	Визуализация: Кабинет-гостевая
60	Развёртка стены А. Кабинет-гостевая (пом. 2)
61	Развёртка стены Б. Кабинет-гостевая (пом. 2)
62	Развёртка стены В. Кабинет-гостевая (пом. 2)
63	Развёртка стены Г. Кабинет-гостевая (пом. 2)
64	Визуализация: Санузел 1 этажа
65	Развёртка стены А. Санузел 1 этажа (пом. 3)
66	Развёртки стен Б, В. Санузел 1 этажа (пом. 3)
67	Развёртка стены Г. Санузел 1 этажа (пом. 3)
68	Визуализация: Котельная
69	Развёртка стены А. Котельная (пом. 4)
70	Развёртки стен Б, Г. Котельная (пом. 4)
71	Визуализация гостиной
72	Визуализация гостиной
73	Визуализация гостиной
74	Развёртка стены А. Гостиная (пом. 5)
75	Развёртка стены Б. Гостиная (пом. 5)
76	Развёртка стены В. Гостиная (пом. 5)
77	Развёртка стены Г. Гостиная (пом. 5)
78	Визуализация: Холл с лестницей
79	Развёртка стены А. Холл с лестницей (пом. 6)
80	Развёртка стены В. Холл с лестницей (пом. 6)
81	Визуализация кладовой
82	Развёртки стен. Кладовая (пом. 7)
83	Визуализация прихожей
84	Визуализация прихожей
85	Развёртка стены А. Прихожая (пом. 8)
86	Развёртка стены Б. Прихожая (пом. 8)
87	Развёртка стены В. Прихожая (пом. 8)
88	Развёртка стены Г. Прихожая (пом. 8)
89	Развёртки стен. Тамбур (пом. 9)
90	Визуализация: Гараж
91	Развёртка стены А. Гараж (пом. 10)
92	Развёртка стены Б. Гараж (пом. 10)
93	Развёртка стены В. Гараж (пом. 10)
94	Развёртка стены Г. Гараж (пом. 10)
95	Визуализация: Веранда
96	Развёртка стены А. Веранда (пом. 11)
97	Развёртка стены В. Веранда (пом. 11)
98	Развёртка стены Г. Веранда (пом. 11)
99	Визуализация: Крыльцо
100	Развёртки стен. Крыльцо (пом. 12)
101	Визуализация: Спальня мастер
102	Визуализация: Спальня мастер
103	Развёртка стены А. Спальня мастер (пом. 13)
104	Развёртка стены Б. Спальня мастер (пом. 13)
105	Развёртка стены В. Спальня мастер (пом. 13)
106	Развёртка стены Г. Спальня мастер (пом. 13)
107	Визуализация: Гардеробная мастер
108	Развёртки стен А, Б. Гардеробная мастер (пом. 14)
109	Развёртки стен В, Г. Гардеробная мастер (пом. 14)
110	Визуализация: Санузел мастер
111	Развёртка стены А. Санузел мастер (пом. 15)
112	Развёртка стены Б. Санузел мастер (пом. 15)
113	Развёртка стены В. Санузел мастер (пом. 15)
114	Развёртка стены Г. Санузел мастер (пом. 15)
115	Визуализация: Спальня 2
116	Визуализация: Спальня 2

	Лист	№ док.	Подпись	Дата
Дизайнер	Кырлан А.О.			19.10.26

Проект: Дом 331 м²


Список листов

Стадия	Лист	Листов
П	2	155

выпуск 18.10.2026 № ffc1f29499 · стр. 2 из 155

Отметки по высоте

±0,000	чистый пол пом. 1, 2, 4–10; отсчёт высот
−0,015	чистый пол пом. 3, ниже на 15 мм
−0,030	чистый пол пом. 11, 12, ниже на 30 мм
плита	верх плиты разный: −0,064, −0,170 (задание на обмер)
сущ. пол	снимается до плиты; не замерен (задание на обмер)

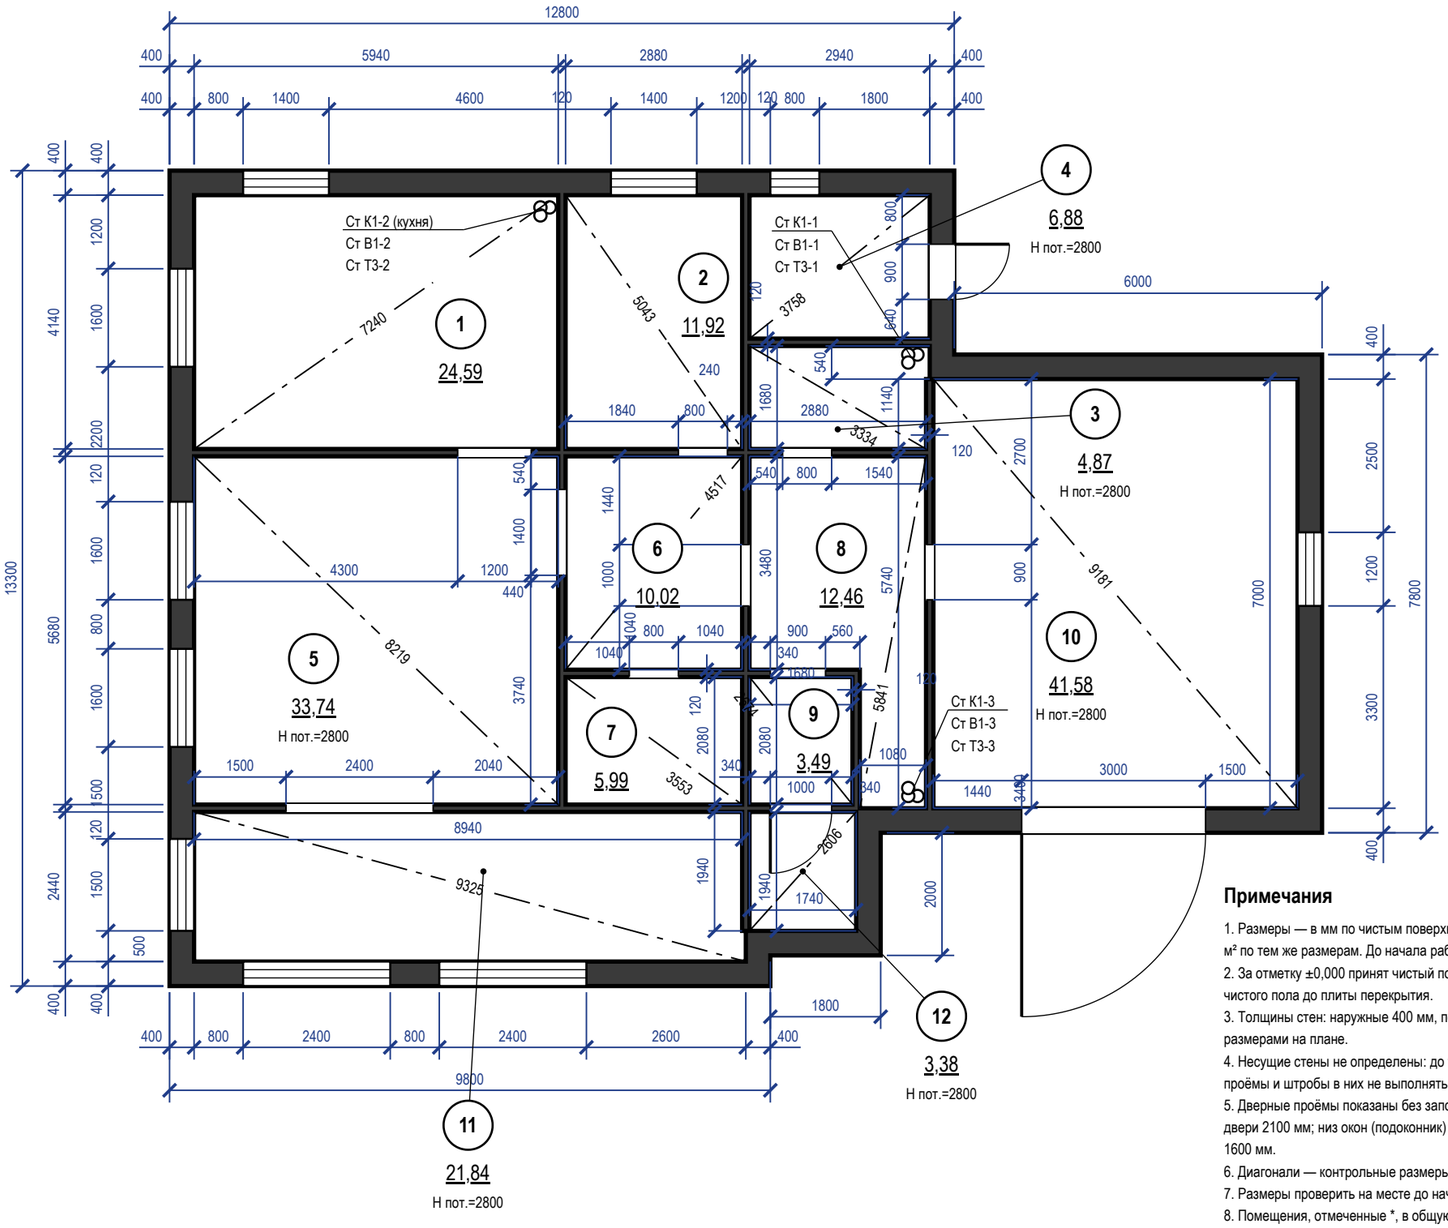

Экспликация помещений

№	Наименование	Площадь, м²
1	Кухня-столовая	24,59
2	Кабинет-гостевая	11,92
3	Санузел 1 этажа	4,87
4	Котельная	6,88
5	Гостиная	33,74
6	Холл с лестницей	10,02
7	Кладовая	5,99
8	Прихожая	12,46
9	Тамбур	3,49
10	Гараж	41,58
11	Веранда *	21,84
12	Крыльцо *	3,38
	Итого (общая площадь)	**270,67**

Условные обозначения

- существующие стены (сечение)
- окно (рама, остекление)
- проём существующий, без заполнения (откосы)
- стояк: К1 — канализация, В1 — ХВС, Т3 — ГВС
- диагональ помещения — контроль прямоугольности
- (1) номер помещения, площадь м²

Примечания

1. Размеры — в мм по чистым поверхностям стен до отделки (по плану заказчика); площади — в м² по тем же размерам. До начала работ выполнить контрольный обмер.
2. За отметку ±0,000 принят чистый пол, не существующий (блок отметок). Н пот. — высота от чистого пола до плиты перекрытия.
3. Толщины стен: наружные 400 мм, перегородки 120 мм; отличающиеся толщины и уступы размерами на плане.
4. Несущие стены не определены: до технического заключения все стены считать несущими; проёмы и штробы в них не выполнять.
5. Дверные проёмы показаны без заполнения; высота дверных проёмов 2100, 2300 мм, проёмов без двери 2100 мм; низ окон (подоконник) 900, 1200 мм от чистого пола, высота окон 1500, 900, 1600 мм.
6. Диагонали — контрольные размеры; расхождение более 5 мм подписать на плане как перекос.
7. Размеры проверить на месте до начала работ; расхождение контрольных промеров ≤ 2 %.
8. Помещения, отмеченные *, в общую площадь квартиры не входят.


					Проект: Дом 331 м²
	Лист	№ док.	Подпись	Дата	План планировки от заказчика · 1-й этаж
Дизайнер	Кырлан А.С.			19.10.26	

Стадия	Лист	Листов
П	3	155

выпуск 18.10.2026 № ffc1f29499 · стр. 3 из 155

Отметки по высоте

±0,000	чистый пол пом. 13, 14, 16–19; отсчёт высот
−0,015	чистый пол пом. 15, 20, ниже на 15 мм
−0,064	верх плиты — расчёт, не замер (задание на обмер)
сущ. пол	снимается до плиты; не замерен (задание на обмер)

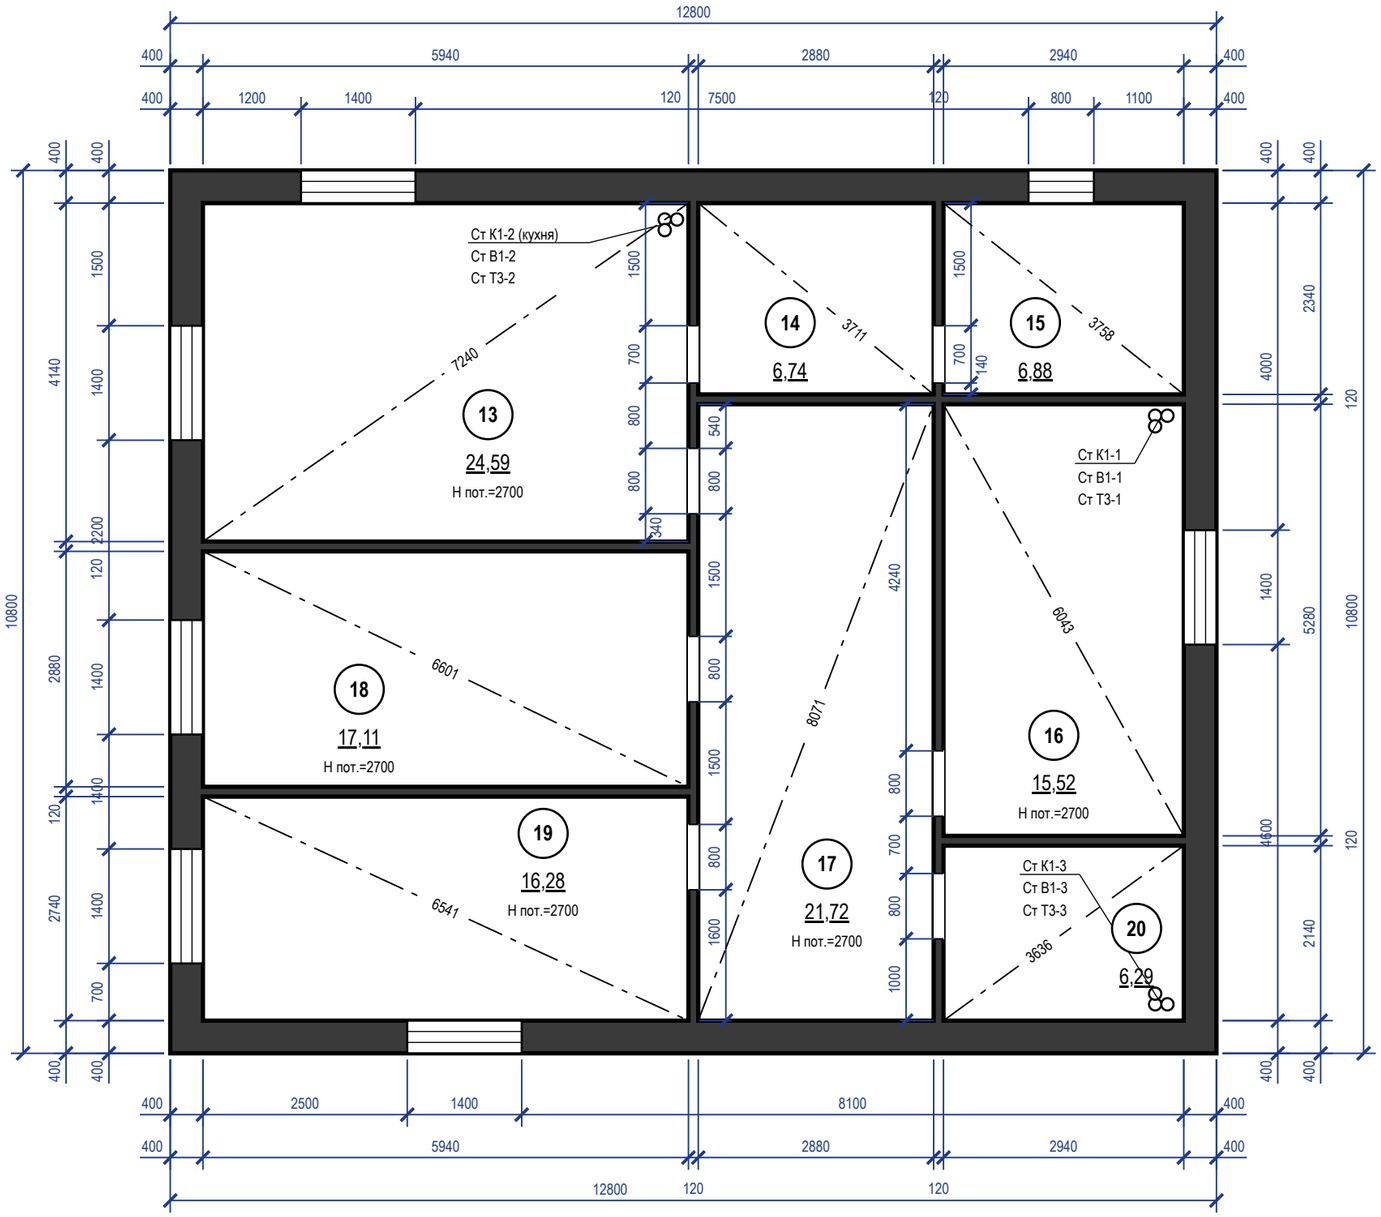

Экспликация помещений

№	Наименование	Площадь, м²
13	Спальня мастер	24,59
14	Гардеробная мастер	6,74
15	Санузел мастер	6,88
16	Спальня 2	15,52
17	Холл мансарды	21,72
18	Спальня 3	17,11
19	Спальня 4	16,28
20	Санузел 2	6,29
	Итого (общая площадь)	**270,67**

Условные обозначения

- существующие стены (сечение)
- окно (рама, остекление)
- проём существующий, без заполнения (откосы)
- стояк: К1 — канализация, В1 — ХВС, Т3 — ГВС
- диагональ помещения — контроль прямоугольности
- (1) номер помещения, площадь м²


Примечания

1. Размеры — в мм по чистым поверхностям стен до отделки (по плану заказчика); площади — в м² по тем же размерам. До начала работ выполнить контрольный обмер.
2. За отметку ±0,000 принят чистый пол, не существующий (блок отметок). Н пот. — высота от чистого пола до плиты перекрытия.
3. Толщины стен: наружные 400 мм, перегородки 120 мм; отличающиеся толщины и уступы размерами на плане.
4. Несущие стены не определены: до технического заключения все стены считать несущими; проёмы и штробы в них не выполнять.
5. Дверные проёмы показаны без заполнения; высота дверных проёмов 2100 мм; низ окон (подоконник) 900, 1500 мм от чистого пола, высота окон 1500, 800 мм.
6. Диагонали — контрольные размеры; расхождение более 5 мм подписать на плане как перекос.
7. Размеры проверить на месте до начала работ; расхождение контрольных промеров ≤ 2 %.

					Проект: Дом 331 м²
	Лист	№ док.	Подпись	Дата	План планировки от заказчика · Мансарда
Дизайнер	Кырлан А.С.			19.10.26	

Стадия	Лист	Листов
П	4	155

выпуск 18.10.2026 № ffc1f29499 · стр. 4 из 155

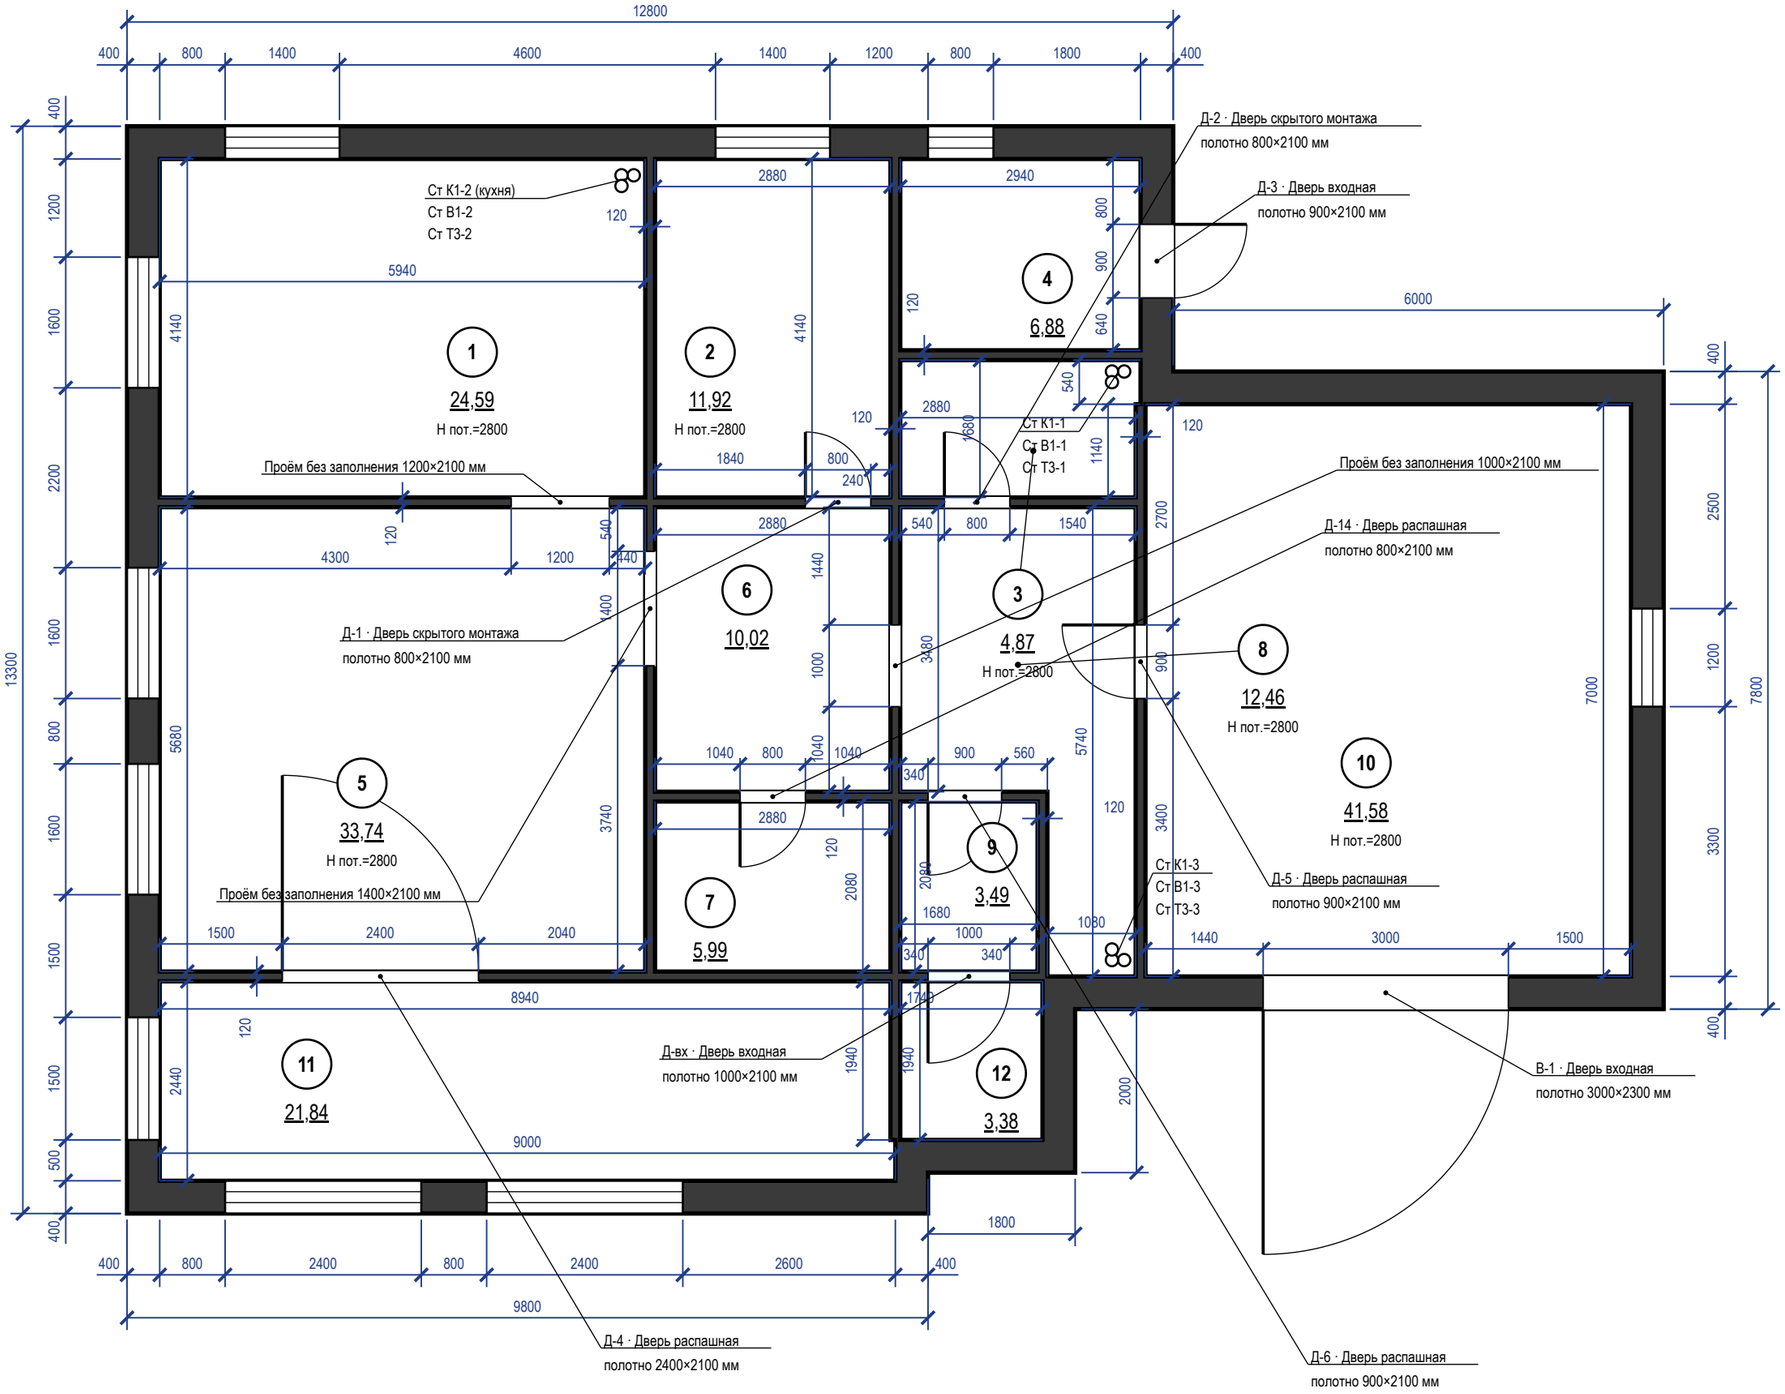

Экспликация помещений

№	Наименование	Площадь, м²
1	Кухня-столовая	24,59
2	Кабинет-гостевая	11,92
3	Санузел 1 этажа	4,87
4	Котельная	6,88
5	Гостиная	33,74
6	Холл с лестницей	10,02
7	Кладовая	5,99
8	Прихожая	12,46
9	Тамбур	3,49
10	Гараж	41,58
11	Веранда *	21,84
12	Крыльцо *	3,38
	Итого (общая площадь)	**270,67**

Примечания

1. Размеры — в мм от чистовых поверхностей стен до отделки; размеры уточнить по месту до начала работ.
2. Новые перегородки и облицовки — синим; каркас и обшивка — по выноскам.
3. Несущие стены не изменять: проёмы, ниши и штробы в них — только по техническому заключению.


					Проект: Дом 331 м²
	Лист	№ док.	Подпись	Дата	План монтажный · 1-й этаж
Дизайнер	Кырлан А.С.			19.10.26	

Стадия	Лист	Листов
П	5	155

выпуск 18.10.2026 · ffc1f29499 · стр. 5 из 155

Экспликация помещений

№	Наименование	Площадь, м²
13	Спальня мастер	24,59
14	Гардеробная мастер	6,74
15	Санузел мастер	6,88
16	Спальня 2	15,52
17	Холл мансарды	21,72
18	Спальня 3	17,11
19	Спальня 4	16,28
20	Санузел 2	6,29
	Итого (общая площадь)	**270,67**

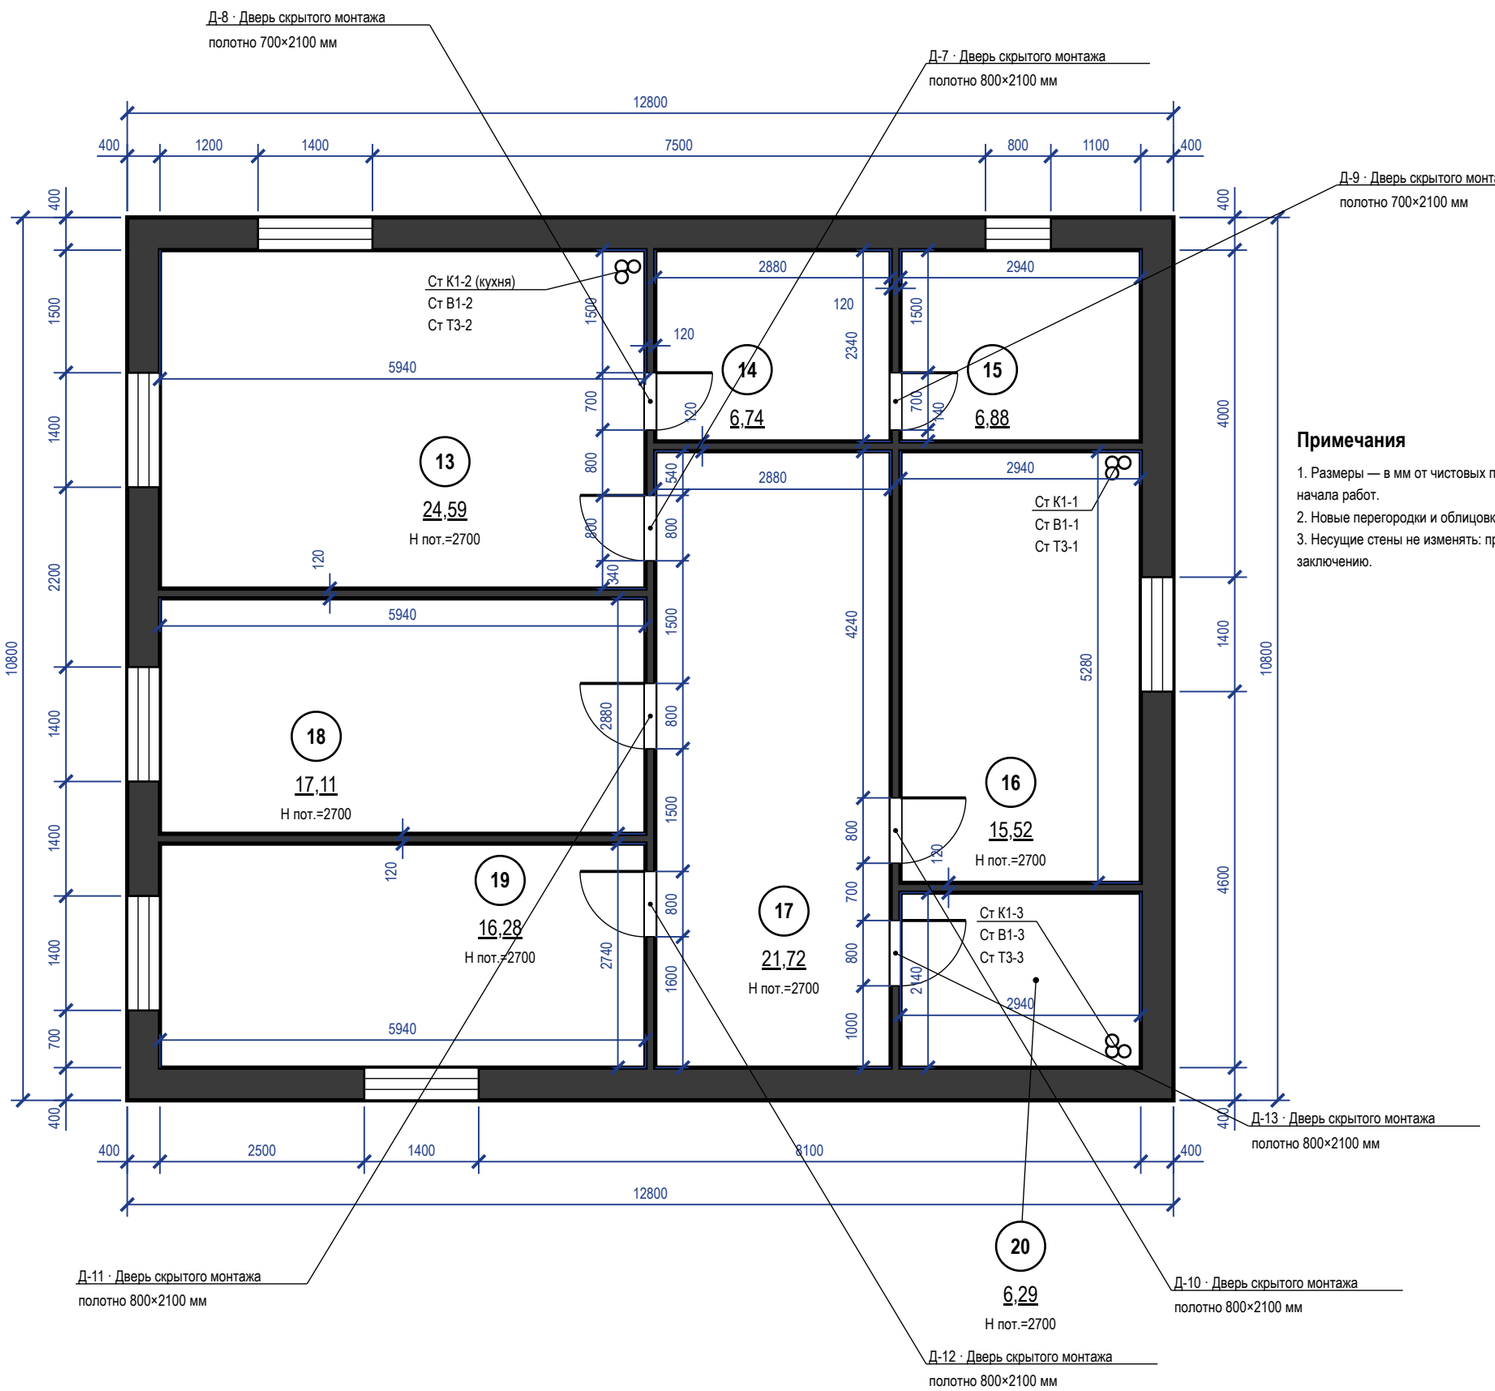

Примечания

1. Размеры — в мм от чистовых поверхностей стен до отделки; размеры уточнить по месту до начала работ.
2. Новые перегородки и облицовки — синим; каркас и обшивка — по выноскам.
3. Несущие стены не изменять: проёмы, ниши и штробы в них — только по техническому заключению.

	Лист	№ док.	Подпись	Дата	
Дизайнер	Кырлан А.С.			19.10.26	


Проект: Дом 331 м²

План монтажный · Мансарда


Стадия	Лист	Листов
П	6	155

выпуск 18.10.2026 № ffc1f29499 · стр. 6 из 155

Привязка выводов и крепление модулей

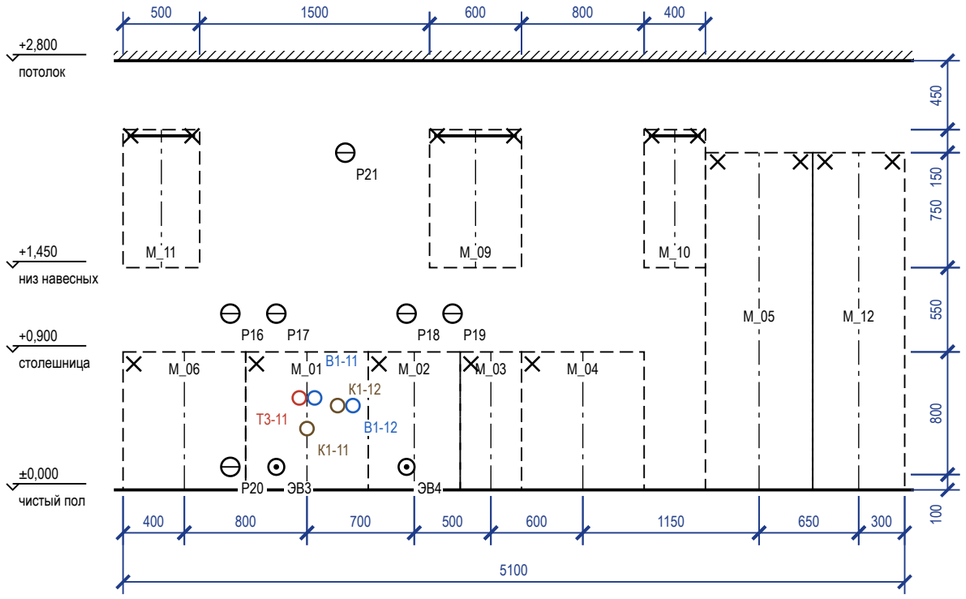

План столешницы

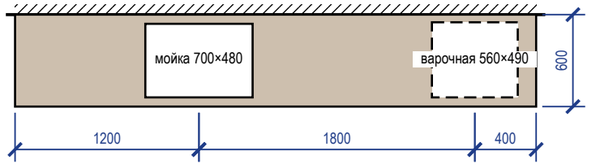

Примечания

1. Выводы — по проекту электрики и ВК; привязка по горизонтали — от оси модуля (плюс — вправо по виду), по высоте — от чистого пола до оси вывода.
2. Пенал — уголки к стене 2 шт. сверху; нижние модули — стяжками между собой и уголком к стене; ряд выставить по уровню опорами цоколя.
3. Розетки над столешницей — не ниже 150 мм над ней и не за корпусом техники; розетка за ПММ, духовым шкафом и холодильником — только в соседнем модуле или в зоне цоколя с доступом.
4. Столешница — вырезы по шаблонам выбранных моделей мойки и варочной панели; торцы у стены — герметик, пристеночный плинтус.

Привязка выводов к осям модулей

Код	Назначение	Модуль	От оси, мм	H, мм	Размещение
P16	розетка ×2 — фартук: мелкая техника	M_06	+300	1150	над столешницей (фартук)
P20	розетка — холодильник встроенный M20 (розетка в модуле M21)	M_06	+300	150	в соседнем модуле, за ящиком
P17	розетка ×2 — фартук: мелкая техника	M_01	−200	1150	над столешницей (фартук)
ЭВ3	вывод кабеля — варочная панель M22	M_01	−200	150	в модуле мойки
T3-11	T3 — межос. 100	M_01	−50	600	в модуле мойки
K1-11	K1 Ø50 — мойка	M_01	0	400	в модуле мойки
B1-11	B1 — межос. 100	M_01	+50	600	в модуле мойки
K1-12	K1 Ø40 — слив ПММ в шкафу мойки	M_01	+200	550	в модуле мойки
P21	розетка — вытяжка M25 (в модуле, съёмная панель)	M_01	+250	2200	над столешницей (фартук)
B1-12	B1 — кран ПММ в шкафу мойки	M_01	+300	550	в модуле мойки
P18	розетка ×2 — фартук: мелкая техника	M_02	−50	1150	над столешницей (фартук)
ЭВ4	вывод кабеля — духовой шкаф M22 (вывод в соседнем модуле M23)	M_02	−50	150	за ПММ — перенести в соседний модуль
P19	розетка ×2 — фартук: мелкая техника	M_02	+250	1150	над столешницей (фартук)

Зазоры под отделку

Поверхность	Отделка	Зазор, мм	Учесть
фартук	керамогранит	10	от чернового основания до корпуса навесных и столешницы
стены	окраска	5	под штукатурку и шпаклёвку за пеналом
пол	инженерная доска		цоколь — после укладки пола, опоры ±20 мм

Условные обозначения

- навесной модуль (невидимый контур)
- ось модуля (от неё — привязка вывода)
- анкер / уголок крепления к стене
- розетка на стене
- вывод кабеля к технике
- B1 — вывод воды B1 / T3, канализации K1

	Лист	№ док.	Подпись	Дата
Дизайнер	Кырлан А.С.			19.10.26


Проект: Дом 331 м²

Кухня (пом. 1). Монтажная схема


Стадия	Лист	Листов
П	7	155

выпуск 18.10.2026 № ffc1f29499 · стр. 7 из 155


Система хранения M_17 (пом. 4)

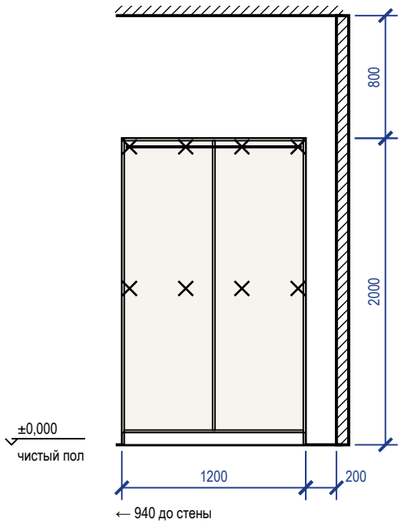


Система хранения M_23 (пом. 7)

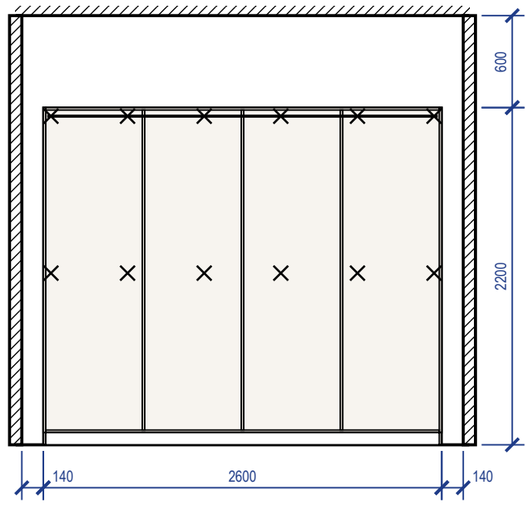

Шкаф-купе M_24 (пом. 8)

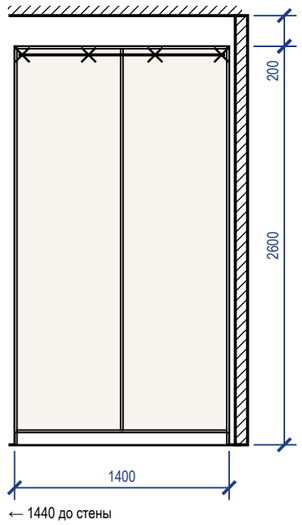

Система хранения M_26 (пом. 10)

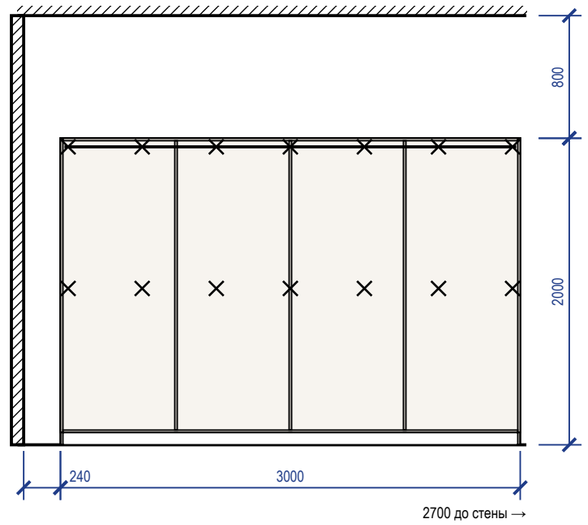

Крепление и зазоры под отделку (изделия листа 1)

Марка	Помещение, стена	Основание	Отделка стены	Зазор, мм	Крепёж по планке	От опрокидывания
M_17	Котельная (4), стена Г	по основанию — см. таблицу крепежа	окраска	5	анкер 8 шт. (2 ряда)	уголки 2 шт.
M_23	Кладовая (7), стена В	по основанию — см. таблицу крепежа	окраска	5	анкер 12 шт. (2 ряда)	уголки 2 шт.
M_24	Прихожая (8), стена А	по основанию — см. таблицу крепежа	окраска	5	анкер 4 шт., шаг 433	уголки 2 шт.
M_26	Гараж (10), стена А	по основанию — см. таблицу крепежа	окраска	5	анкер 14 шт. (2 ряда)	true

Крепёж по основанию стены

Основание стены	Крепёж
бетон, ж/б	анкер-шуруп 7,5×72 или дюбель 8×60 с шурупом 5×70
кирпич полнотелый	дюбель 8×80 с шурупом 5×90
газобетон, пазогребень	дюбель для газобетона 10×100 или химический анкер
гипсокартон	закладная до обшивки (брус 40×80 или фанера 18 мм), саморез в закладную

Условные обозначения

- анкер / уголок крепления к стене
- корпус и полки ЛДСП (вид на стену)
- компенсатор — короб до потолка


Примечания

1. Установочные размеры — от чистого пола и чистых стен; перед установкой контрольный замер после отделки.
2. Порядок: корпус выставить по уровню опорами цоколя → закрепить к стене по задней планке → навесить двери и фасады, отрегулировать зазоры → подогнать и закрепить компенсатор.
3. Анкеры — с шагом не более 500 мм, не ближе 50 мм от края планки; на ГКЛ только в закладную, установленную до обшивки.
4. Скрытые коммуникации под анкеры проверить детектором; трассы электрики по плану розеток.
5. Монтажная схема на 2 листах, лист 1 из 2; продолжение — на следующем листе схемы. Условные обозначения, таблица крепежа по основанию и примечания повторены на каждом листе.


					Проект: Дом 331 м²	
	Лист	№ док.	Подпись	Дата	Шкафы. Монтажная схема. Лист 1 из 2	Стадия / Лист / Листов
Дизайнер	Кырлан А.С.			19.10.26		П / 8 / 155

выпуск 18.10.2026 № ffc1f29499 · стр. 8 из 155


Система хранения М_43 пом. 14

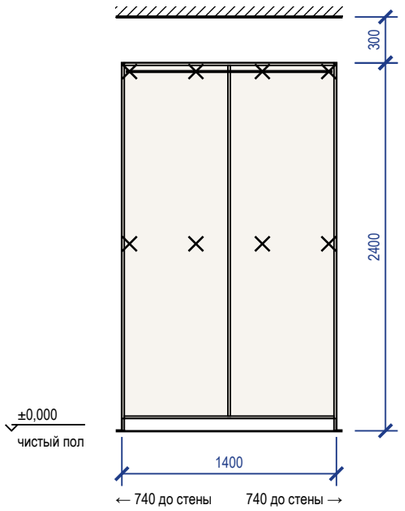


Шкаф распашной М_46 (пом. 16)

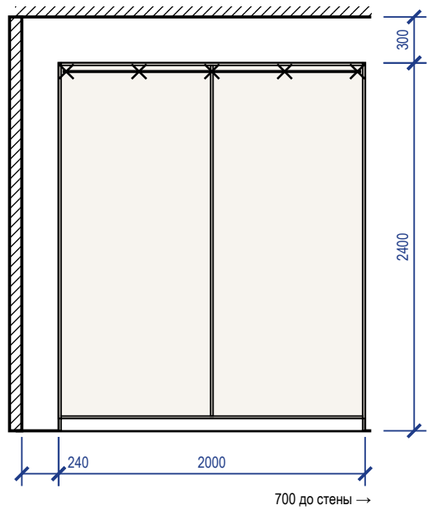


Система хранения М_49 (пом. 17)

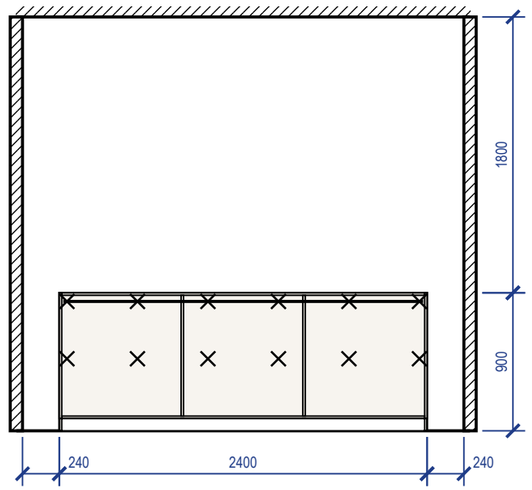

Шкаф распашной М_53 (пом. 18)

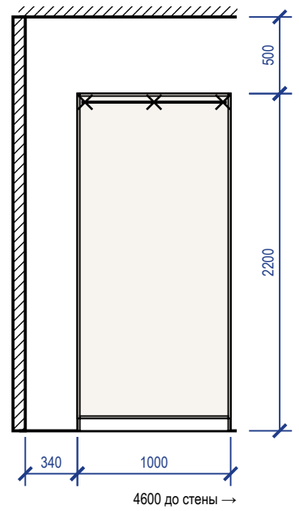

Шкаф распашной М_56 пом. 19

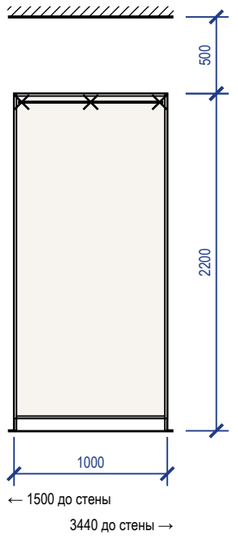

Крепление и зазоры под отделку (изделия листа 2)

Марка	Помещение, стена	Основание	Отделка стены	Зазор, мм	Крепёж по планке	От опрокидывания
М_43	Гардеробная мастер (14), стена В	по основанию — см. таблицу крепежа	окраска	5	анкер 8 шт. (2 ряда)	уголки 2 шт.
М_46	Спальня 2 (16), стена А	по основанию — см. таблицу крепежа	окраска	5	анкер 5 шт., шаг 475	уголки 2 шт.
М_49	Холл мансарды (17), стена В	по основанию — см. таблицу крепежа	окраска	5	анкер 12 шт. (2 ряда)	true
М_53	Спальня 3 (18), стена В	по основанию — см. таблицу крепежа	окраска	5	анкер 3 шт., шаг 450	уголки 2 шт.
М_56	Спальня 4 (19), стена А	по основанию — см. таблицу крепежа	окраска	5	анкер 3 шт., шаг 450	уголки 2 шт.

Крепёж по основанию стены

Основание стены	Крепёж
бетон, ж/б	анкер-шуруп 7,5×72 или дюбель 8×60 с шурупом 5×70
кирпич полнотелый	дюбель 8×80 с шурупом 5×90
газобетон, пазогребень	дюбель для газобетона 10×100 или химический анкер
гипсокартон	закладная до обшивки (брус 40×80 или фанера 18 мм), саморез в закладную

Условные обозначения


- × — анкер / уголок крепления к стене
- ▭ — корпус и полки ЛДСП (вид на стену)
- ▨ — компенсатор — короб до потолка

Примечания

1. Установочные размеры — от чистого пола и чистых стен; перед установкой контрольный замер после отделки.
2. Порядок: корпус выставить по уровню опорами цоколя → закрепить к стене по задней планке → навесить двери и фасады, отрегулировать зазоры → подогнать и закрепить компенсатор.
3. Анкеры — с шагом не более 500 мм, не ближе 50 мм от края планки; на ГКЛ только в закладную, установленную до обшивки.
4. Скрытые коммуникации под анкеры проверить детектором; трассы электрики по плану розеток.
5. Монтажная схема на 2 листах, лист 2 из 2. Условные обозначения, таблица крепежа по основанию и примечания повторены на каждом листе.

					Проект: Дом 331 м²	
	Лист	№ док.	Подпись	Дата	Шкафы. Монтажная схема. Лист 2 из 2	Стадия / Лист / Листов
Дизайнер	Кырлан А.С.			19.10.26		П / 9 / 155

выпуск 18.10.2026 № ffc1f29499 · стр. 9 из 155

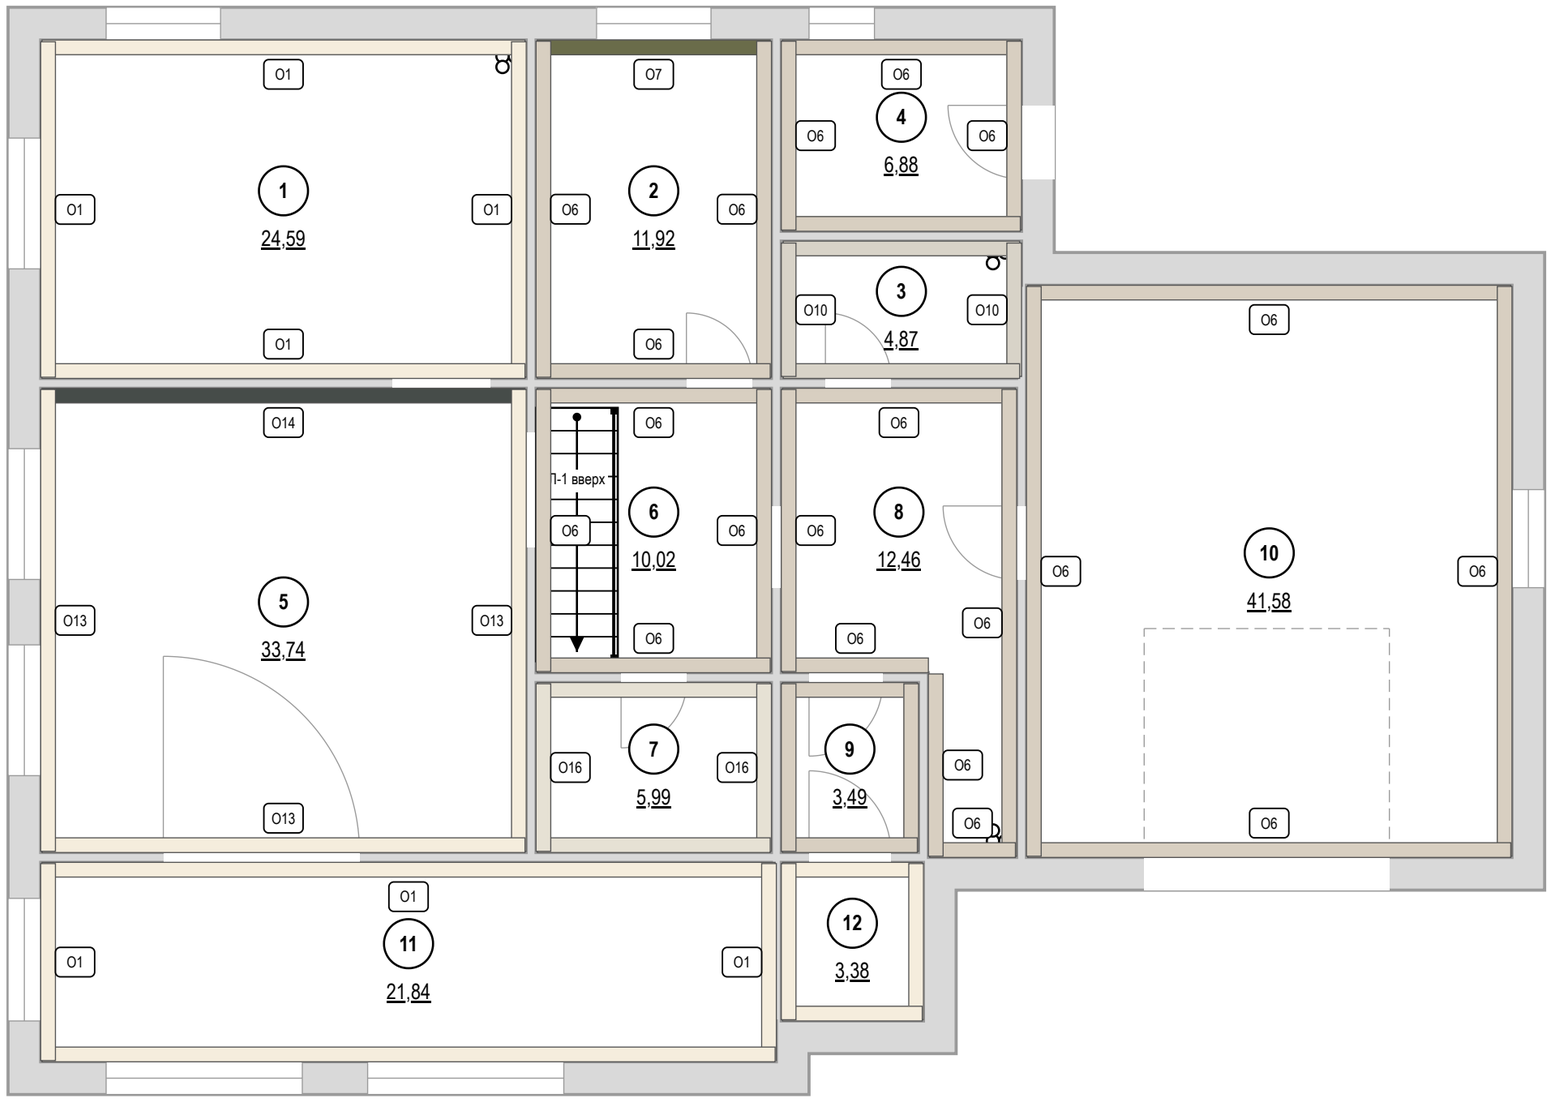


Покрытия стен

Марка	Покрытие	Помещение: S, м²	Итого, м²
О1	окраска Tikkurila · S 0804-Y30R «S 0804-Y30R»	1: 47,0; 11: 49,3; 12: 18,4	114,7
О6	окраска Farrow & Ball · No. 226 «Joa's White»	2: 29,3; 4: 26,6; 6: 26,9; 8: 40,3; 9: 16,7; 10: 62,3	202,1
О7	окраска Farrow & Ball · No. 298 «Bancha»	2: 5,9	5,9
О10	облицовка плиткой Atlas Concorde · A8UZ «Marvel Travertine» 600×1200 мм	3: 20,1	20,1
О13	окраска Tikkurila · S 0804-Y30R «S 0804-Y30R»	5: 35,4	35,4
О14	окраска Tikkurila · No. 93 «Studio Green — почти чёрный зелёный»	5: 14,0	14,0
О16	окраска Tikkurila · No. 105 «Slaked Lime»	7: 25,8	25,8

					Проект: Дом 331 м²
	Лист	№ док.	Подпись	Дата	
Дизайнер	Кырлан А.С.			19.10.26	Карта покрытий стен · 1-й этаж

Стадия	Лист	Листов
П	10	155

выпуск 18.10.2026 № ffc1f29499 · стр. 10 из 155

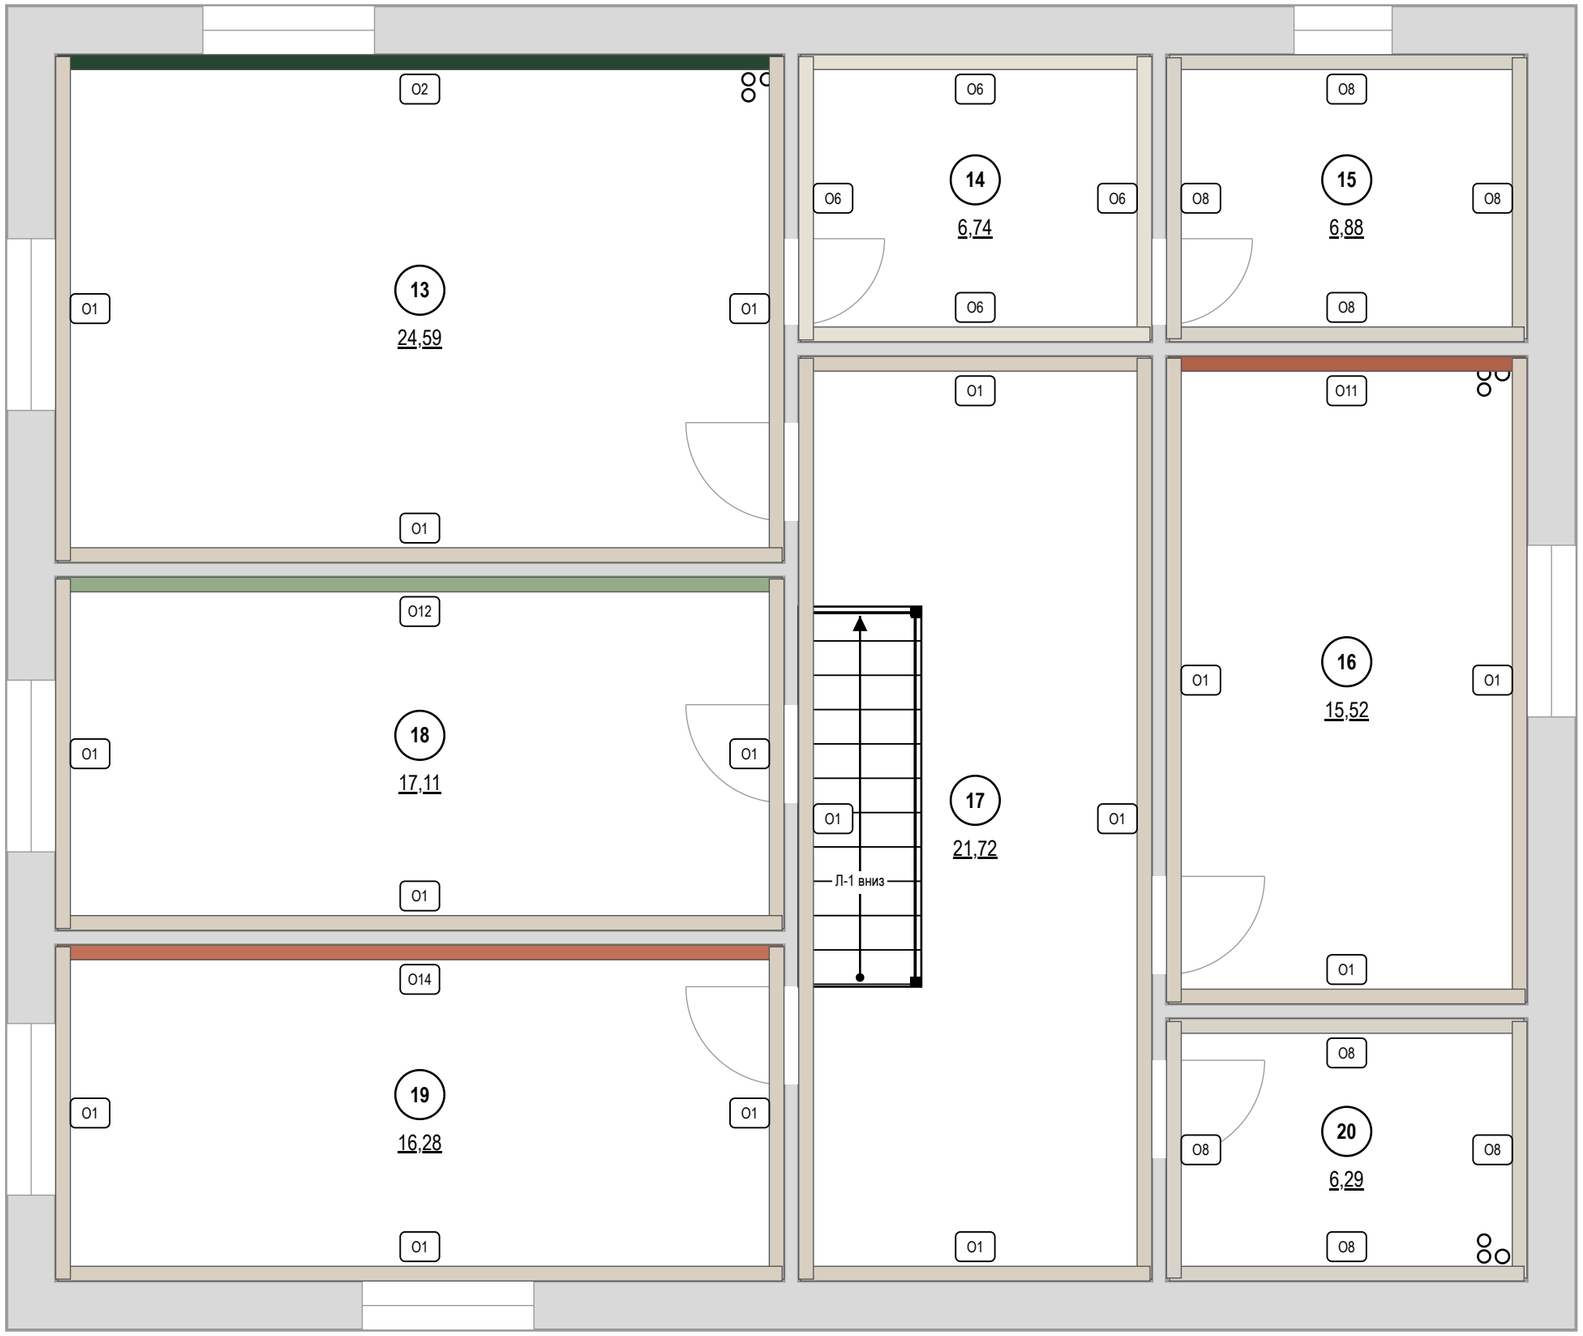

Покрытия стен

Марка	Покрытие	Помещение: S, м²	Итого, м²
О1	окраска Farrow & Ball · No. 226 «Joa's White»	13: 32,9; 16: 32,4; 17: 47,5; 18: 27,6; 19: 24,7	165,2
О2	окраска Farrow & Ball · S 7020-G10Y «Хвойный тёмно-зелёный»	13: 13,9	13,9
О6	окраска Tikkurila · No. 105 «Slaked Lime»	14: 24,9	24,9
О8	облицовка плиткой Atlas Concorde · A8UZ «Marvel Travertine» 600×1200 мм	15: 22,8; 20: 22,3	45,1

					Проект: Дом 331 м²
	Лист	№ док.	Подпись	Дата	Карта покрытий стен · Мансарда
Дизайнер	Кырлан А.С.			19.10.26	Стадия: П; Лист: 11; Листов: 155

выпуск 18.10.2026 № ffc1f29499 · стр. 11 из 155

Колерная карта по помещениям

Помещение	Поверхность	Образец	Поз.	Система и код цвета	Производитель, линейка / материал, артикул	Блеск	Класс EN 13300	LRV	Площадь
1. Кухня-столовая 24,59 м²	стены		**К1**	NCS S 0804-Y30R	Tikkurila · Luja 7	полуматов.	1	85	47,0 м²
	потолок		**К2**	NCS S 0804-Y30R	Tikkurila · Luja 7	матовая	1	85	24,6 м²
	пол		**КМ1**	по образцу	Coswick · Вековые традиции				24,6 м²
	плинтус		**К3**	NCS S 0804-Y30R	МДФ · в цвет NCS	полуглянц.	2	85	18,3 м
	фартук		**КМ2**	тон Paper F497 (тёплый белый)	керамогранит · аналог по хар.				0,9 м²
2. Кабинет-гостевая 11,92 м²	стены		**К4**	Farrow & Ball No. 226	Farrow & Ball · Modern Emulsion	матовая	1	63	26,4 м²
	акцент А		**К5**	Farrow & Ball No. 298	Farrow & Ball · Modern Emulsion	матовая	1	14	6,0 м²
	потолок		**К6**	Little Greene No. 105	Tikkurila · Anti-Reflex 2	глубокомат.	2	82	11,9 м²
	пол		**КМ1**	по образцу	Coswick · Вековые традиции				11,9 м²
	плинтус		**К7**	Farrow & Ball No. 226	МДФ · в цвет Farrow & Ball			63	11,7 м
3. Санузел 1 этажа 4,87 м²	стены		**К8**	Atlas Concorde A8UZ	Atlas Concorde · Marvel Travertine				20,5 м²
	потолок		**К9**	Little Greene No. 105	Tikkurila · Luja 7	матовая	1	82	4,9 м²
	пол		**К8**	Atlas Concorde A8UZ	Atlas Concorde · Marvel Travertine				4,9 м²
4. Котельная 6,88 м²	стены		**К4**	Farrow & Ball No. 226	Farrow & Ball · Modern Emulsion	матовая	1	63	27,0 м²
	потолок		**К6**	Little Greene No. 105	Tikkurila · Anti-Reflex 2	глубокомат.	2	82	6,9 м²
	пол		**К8**	Atlas Concorde A8UZ	Atlas Concorde · Marvel Travertine				6,9 м²
	плинтус		**К7**	Farrow & Ball No. 226	МДФ · в цвет Farrow & Ball			63	9,7 м
5. Гостиная 33,74 м²	стены		**К10**	NCS S 0804-Y30R	Tikkurila · Optiva 5 Matt	матовая	2	85	35,7 м²
	акцент А		**К11**	Farrow & Ball No. 93	Tikkurila · Optiva 5 Matt	матовая	2	7	14,1 м²
	потолок		**К12**	NCS S 0804-Y30R	Tikkurila · Anti-Reflex 2	глубокомат.	2	85	33,7 м²
	пол		**КМ1**	по образцу	Coswick · Вековые традиции				33,7 м²
	плинтус		**К3**	NCS S 0804-Y30R	МДФ · в цвет NCS	полуглянц.	2	85	18,2 м
6. Холл с лестницей 10,02 м²	стены		**К4**	Farrow & Ball No. 226	Farrow & Ball · Modern Emulsion	матовая	1	63	23,6 м²
	потолок		**К6**	Little Greene No. 105	Tikkurila · Anti-Reflex 2	глубокомат.	2	82	10,0 м²
	пол		**КМ1**	по образцу	Coswick · Вековые традиции				10,0 м²
	плинтус		**К7**	Farrow & Ball No. 226	МДФ · в цвет Farrow & Ball			63	7,0 м
7. Кладовая 5,99 м²	стены		**К13**	Little Greene No. 105	Tikkurila · Harmony	матовая	1	82	23,3 м²
	потолок		**К6**	Little Greene No. 105	Tikkurila · Anti-Reflex 2	глубокомат.	2	82	6,0 м²
	пол		**КМ1**	по образцу	Coswick · Вековые традиции				6,0 м²
	плинтус		**К14**	Little Greene No. 105	МДФ · в цвет Little Greene			82	7,8 м
8. Прихожая 12,46 м²	стены		**К4**	Farrow & Ball No. 226	Farrow & Ball · Modern Emulsion	матовая	1	63	40,7 м²
	потолок		**К6**	Little Greene No. 105	Tikkurila · Anti-Reflex 2	глубокомат.	2	82	12,5 м²
	пол		**К8**	Atlas Concorde A8UZ	Atlas Concorde · Marvel Travertine				12,5 м²
	плинтус		**К7**	Farrow & Ball No. 226	МДФ · в цвет Farrow & Ball			63	13,6 м
9. Тамбур 3,49 м²	стены		**К4**	Farrow & Ball No. 226	Farrow & Ball · Modern Emulsion	матовая	1	63	17,1 м²
	потолок		**К6**	Little Greene No. 105	Tikkurila · Anti-Reflex 2	глубокомат.	2	82	3,5 м²
	пол		**К8**	Atlas Concorde A8UZ	Atlas Concorde · Marvel Travertine				3,5 м²
	плинтус		**К7**	Farrow & Ball No. 226	МДФ · в цвет Farrow & Ball			63	5,6 м
10. Гараж 41,58 м²	стены		**К4**	Farrow & Ball No. 226	Farrow & Ball · Modern Emulsion	матовая	1	63	62,6 м²
	потолок		**К6**	Little Greene No. 105	Tikkurila · Anti-Reflex 2	глубокомат.	2	82	41,6 м²
	пол		**КМ3**	по образцу	ероху · аналог по хар.				41,6 м²
	плинтус		**КМ4**	по образцу	pvc · аналог по хар.				22,0 м

Примечания

1. Цвет утверждается только по выкрасу на объекте: формат от А3 до 1000×1000 мм на загрунтованном ГКЛ, в 2 слоя (как на стене), не на белой шпаклёвке; смотреть днём и при свете проекта своего помещения, рядом с образцами пола и фасадов. Подпись на обороте: код, бренд и веер, дата.
2. Колеровка машинная в колеровочном центре бренда; каждый код — за один проход, одной партией на весь объём. Колеровщику передаётся только система и код утверждённого веера; плашки и HEX на листе — ориентир, печать не является эталоном цвета.
3. Класс мокрого истирания — EN 13300 (ISO 11998); блеск — по ГОСТ 31975 (ISO 2813), геометрия 60°. LRV — пересчёт координаты L каталога производителя (Y = ((L*+16)/116)³); «≈» — расчёт по HEX, справочно.
4. Площади поверхностей — тем же способом и с теми же цифрами, что в ведомости отделки (способ счёта — в общих указаниях); объём краски к заказу, фасовка и материалы КМ — в спецификации отделочных материалов.
5. Колерная карта на 2 листах: обозначения повторены на каждом, схема квартиры и палитра — на первом, перечень выкрасов — на последнем.

Схема палитры проекта


Стиль: Шале 60% + Эко и органический модерн 40% · схема: complement

основной Farrow & Ball No. 226	основной NCS S 0804-Y30R	основной Little Greene No. 105	второстепенный Tikkurila V451	второстепенный NCS S 3020-G30Y	второстепенный Tikkurila X463	второстепенный Farrow & Ball No. 229	второстепенный Farrow & Ball No. 40	второстепенный Farrow & Ball No. 241	второстепенный NCS S 2005-Y20R	второстепенный NCS S 3010-Y30R	акцентный NCS S 7020-G10Y	акцентный Farrow & Ball No. 64	акцентный Farrow & Ball No. 43
Joa's White LRV 63 стены 2,4,6,8,9,10,13,16,17,18,19; плинтус 3,4,6,8,9,10,11,12,15,16; потолок 5,9	тёплый молочный белый LRV 85 стены 1,5,11,12; потолок 1,5,11,12; плинтус 5,9	Slaked Lime LRV 82 потолок 2,3,4,6,7,8,9,10,11,12,15,16,18; стены 7,14; плинтус 7,14; высокий плинтус 10,16	Olive grove V451 LRV 51 текстиль/декор 18	шалфей LRV 38 акцент 18; текстиль/декор 17,18	Sandstone X463 LRV 51 текстиль/декор 2,16,19	Elephant's foot — тёплый средне-песочный оттенок LRV 52 текстиль/декор 13	Mouse's foot — тёплый серо-бежевый LRV 26 текстиль/декор 2	Charleston Grey — серо-коричневый с нюансом хаки LRV 30 текстиль/декор 5,10	Светлый песочно-серый LRV 60 текстиль/декор 1,5,13,18,19	орех/лён тёмный LRV 43 текстиль/декор 2,16,19	Хвойный тёмно-зелёный LRV ≈5 акцент 13; текстиль/декор 13	Red Earth LRV 18 акцент 16; текстиль/декор 16	Eating Room Red — тёплый серый LRV 11.8 в отделке не применён

План 60/30/10



Окраска, факт — по площади стен, акцентов, потолков

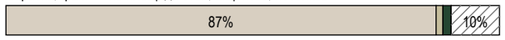

окрашено всего 963,9 м²; второстепенный тон несут мебель и текстиль

Условные обозначения

- **К1** NCS S 0804-Y30R · тёплый молочный белый · Tikkurila Luja 7 · полуматов. · кл. 1
- **К2** NCS S 0804-Y30R · тёплый молочный белый · Tikkurila Luja 7 · матовая · кл. 1
- **К3** NCS S 0804-Y30R · тёплый молочный белый · МДФ · полуглянц. · кл. 2
- **К4** Farrow & Ball No. 226 · Joa's White · Modern Emulsion · матовая · кл. 1
- **К5** Farrow & Ball No. 298 · Bancha · Modern Emulsion · матовая · кл. 1
- **К6** Little Greene No. 105 · Slaked Lime · Anti-Reflex 2 · глубокомат. · кл. 2
- **К7** Farrow & Ball No. 226 · Joa's White · МДФ
- **К8** Atlas Concorde A8UZ · Marvel Travertine · Marvel Travertine
- **К9** Little Greene No. 105 · Slaked Lime · Luja 7 · матовая · кл. 1
- **К10** NCS S 0804-Y30R · тёплый молочный белый · Tikkurila Optiva 5 Matt · матовая · кл. 2
- **К11** Farrow & Ball No. 93 · Studio Green — почти чёрный зелёный · Optiva 5 Matt · матовая · кл. 2
- **К12** NCS S 0804-Y30R · тёплый молочный белый · Tikkurila Anti-Reflex 2 · глубокомат. · кл. 2
- **К13** Little Greene No. 105 · Slaked Lime · Harmony · матовая · кл. 1
- **К14** Little Greene No. 105 · Slaked Lime · МДФ
- **К15** NCS S 7020-G10Y · Хвойный тёмно-зелёный · Farrow & Ball Modern Emulsion · матовая · кл. 1
- **К16** Farrow & Ball No. 64 · Red Earth · Modern Emulsion · матовая · кл. 1
- **К17** NCS S 3020-G30Y · шалфей · Farrow & Ball Modern Emulsion · матовая · кл. 1
- **К18** Farrow & Ball No. 226 · Joa's White · Contour (Luxxus)
- **К19** NCS S 3040-Y70R · обожжённая глина · Farrow & Ball Modern Emulsion · матовая · кл. 1
- **КМ1** инженерная доска · 1167-4250
- **КМ2** аналог: керамогранит матовый, тон F497, 600×600×9 мм
- **КМ3** ероху · аналог: наливной полимерный пол (эпоксидный), с кварцевой посыпкой, 3 мм
- **КМ4** pvc · аналог: плинтус ПВХ влагостойкий 100 мм, серый
- **КМ5** керамогранит · A8UZ
- **КМ6** керамогранит · аналог: плинтус из керамогранита пола, подрезка 80 мм, верхняя кромка с запилом 45°


- дерево (доска, паркет, ламинат) — рисунок досок
- керамогранит, плитка, камень — сетка швов по формату
- материал без кода цвета — по образцу (артикул в ведомости отделки)
- HEX не задан — цвет только по коду и вееру

К — позиция окраски (код + продукт + блеск), КМ — позиция материала, тон КМ — по описанию артикула, эталон — образец материала; ≈ LRV — расчёт по HEX, справочно

					Проект: Дом 331 м²
	Лист	№ док.	Подпись	Дата	
Дизайнер	Кырлан А.С.			19.10.26	Колерная карта

Стадия	Лист	Листов
П	12	155

выпуск 18.10.2026 № ffc1f29499 · стр. 12 из 155

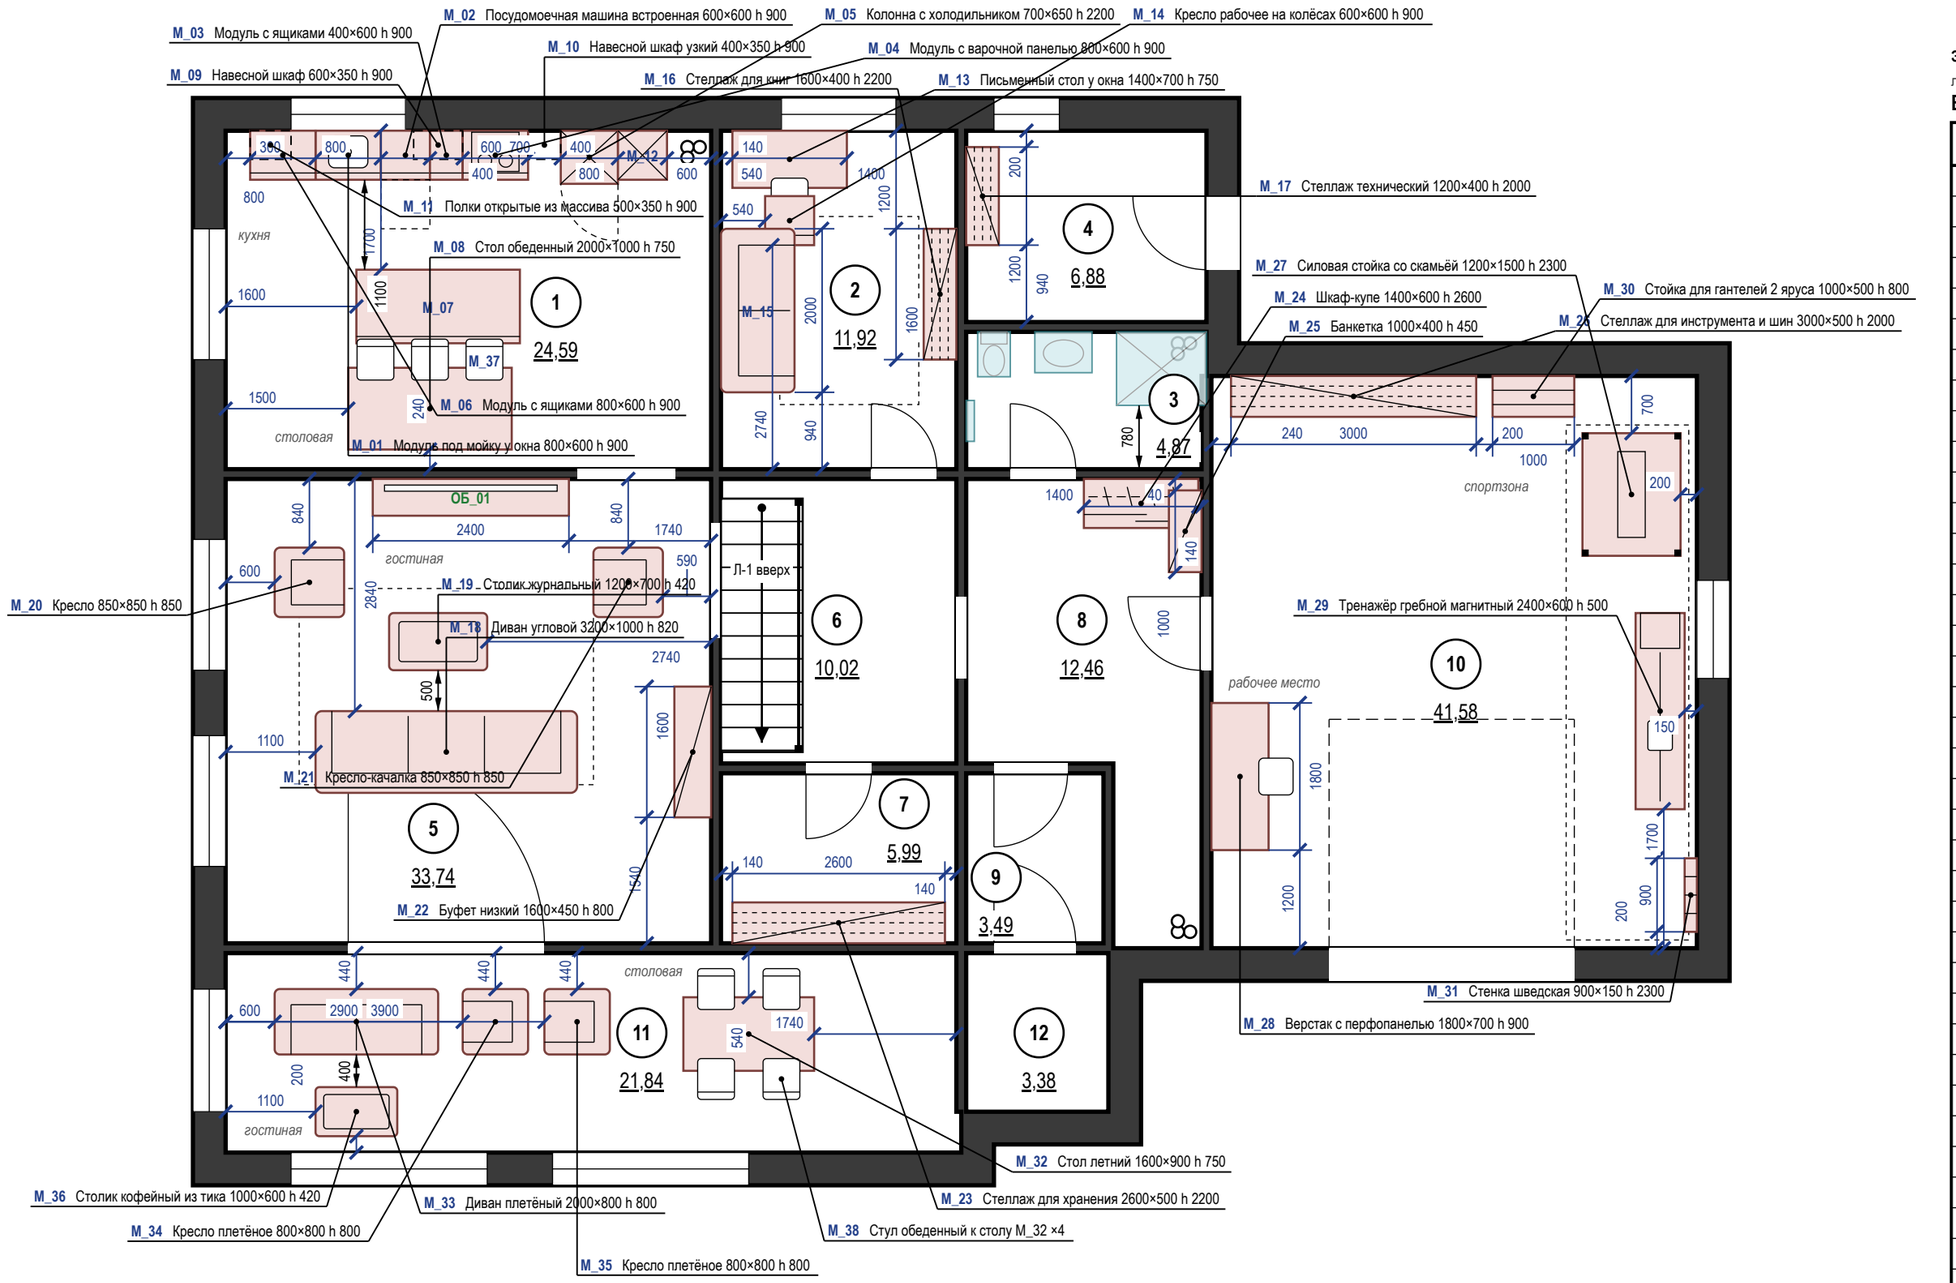

Экспликация помещений

лист обмерного плана · на плане — номера в марках

Ведомость мебели и оборудования

Марка	Наименование	Ш×Г×В, мм	Пом.	Кол.
M_01	Модуль под мойку у окна	800×600×900	1	1
M_02	Посудомоечная машина встроенная	600×600×900	1	1
M_03	Модуль с ящиками	400×600×900	1	1
M_04	Модуль с варочной панелью	800×600×900	1	1
M_05	Колонна с холодильником	700×650×2200	1	1
M_06	Модуль с ящиками	800×600×900	1	1
M_07	Остров с барной консолью	2000×900×900	1	1
M_08	Стол обеденный 2000×1000	2000×1000×750	1	1
M_09	Навесной шкаф	600×350×900	1	1
M_10	Навесной шкаф узкий	400×350×900	1	1
M_11	Полки открытые из массива	500×350×900	1	1
M_12	Пенал-кладовая с выдвижными корзинами	600×600×2200	1	1
M_13	Письменный стол у окна	1400×700×750	2	1
M_14	Кресло рабочее на колёсах	600×600×900	2	1
M_15	Диван-кровать гостевой	2000×900×850	2	1
M_16	Стеллаж для книг	1600×400×2200	2	1
M_17	Стеллаж технический	1200×400×2000	4	1
ОБ_01	ТВ-стена с камином	2400×450×600	5	1
M_18	Диван угловой	3200×1000×820	5	1
M_19	Столик журнальный	1200×700×420	5	1
M_20	Кресло	850×850×850	5	1
M_21	Кресло-качалка	850×850×850	5	1
M_22	Буфет низкий	1600×450×800	5	1
M_23	Стеллаж для хранения	2600×500×2200	7	1
M_24	Шкаф-купе	1400×600×2600	8	1
M_25	Банкетка	1000×400×450	8	1
M_26	Стеллаж для инструмента и шин	3000×500×2000	10	1
M_27	Силовая стойка со скамьёй	1200×1500×2300	10	1
M_28	Верстак с перфопанелью	1800×700×900	10	1
M_29	Тренажёр гребной магнитный	2400×600×500	10	1
M_30	Стойка для гантелей 2 яруса	1000×500×800	10	1
M_31	Стенка шведская	900×150×2300	10	1
M_32	Стол летний	1600×900×750	11	1
M_33	Диван плетёный	2000×800×800	11	1
M_34	Кресло плетёное	800×800×800	11	1
M_35	Кресло плетёное	800×800×800	11	1
M_36	Столик кофейный из тика	1000×600×420	11	1
M_37	Стул обеденный к столу M_08	450×500×820	1	3
M_38	Стул обеденный к столу M_32	450×500×820	11	4

Ш — вдоль стены (изголовья), Г — от стены (длина кровати)

Материалы, модели, допуск замены — лист 15


Примечания

1. Размеры — в мм от чистовых поверхностей стен; размеры мебели уточнить после отделочных работ; общие указания — лист 2.
2. Стулья обеденной группы (M_37 — 3 шт., M_38 — 4 шт.) показаны в рабочем положении, задвинутыми под столешницу на 150 мм.

					Проект: Дом 331 м²
	Лист	№ док.	Подпись	Дата	План размещения мебели и оборудования · 1-й этаж
Дизайнер	Кырлан А.С.			19.10.26	

Стадия	Лист	Листов
П	13	155

выпуск 18.10.2026 № ffc1f29499 · стр. 13 из 155

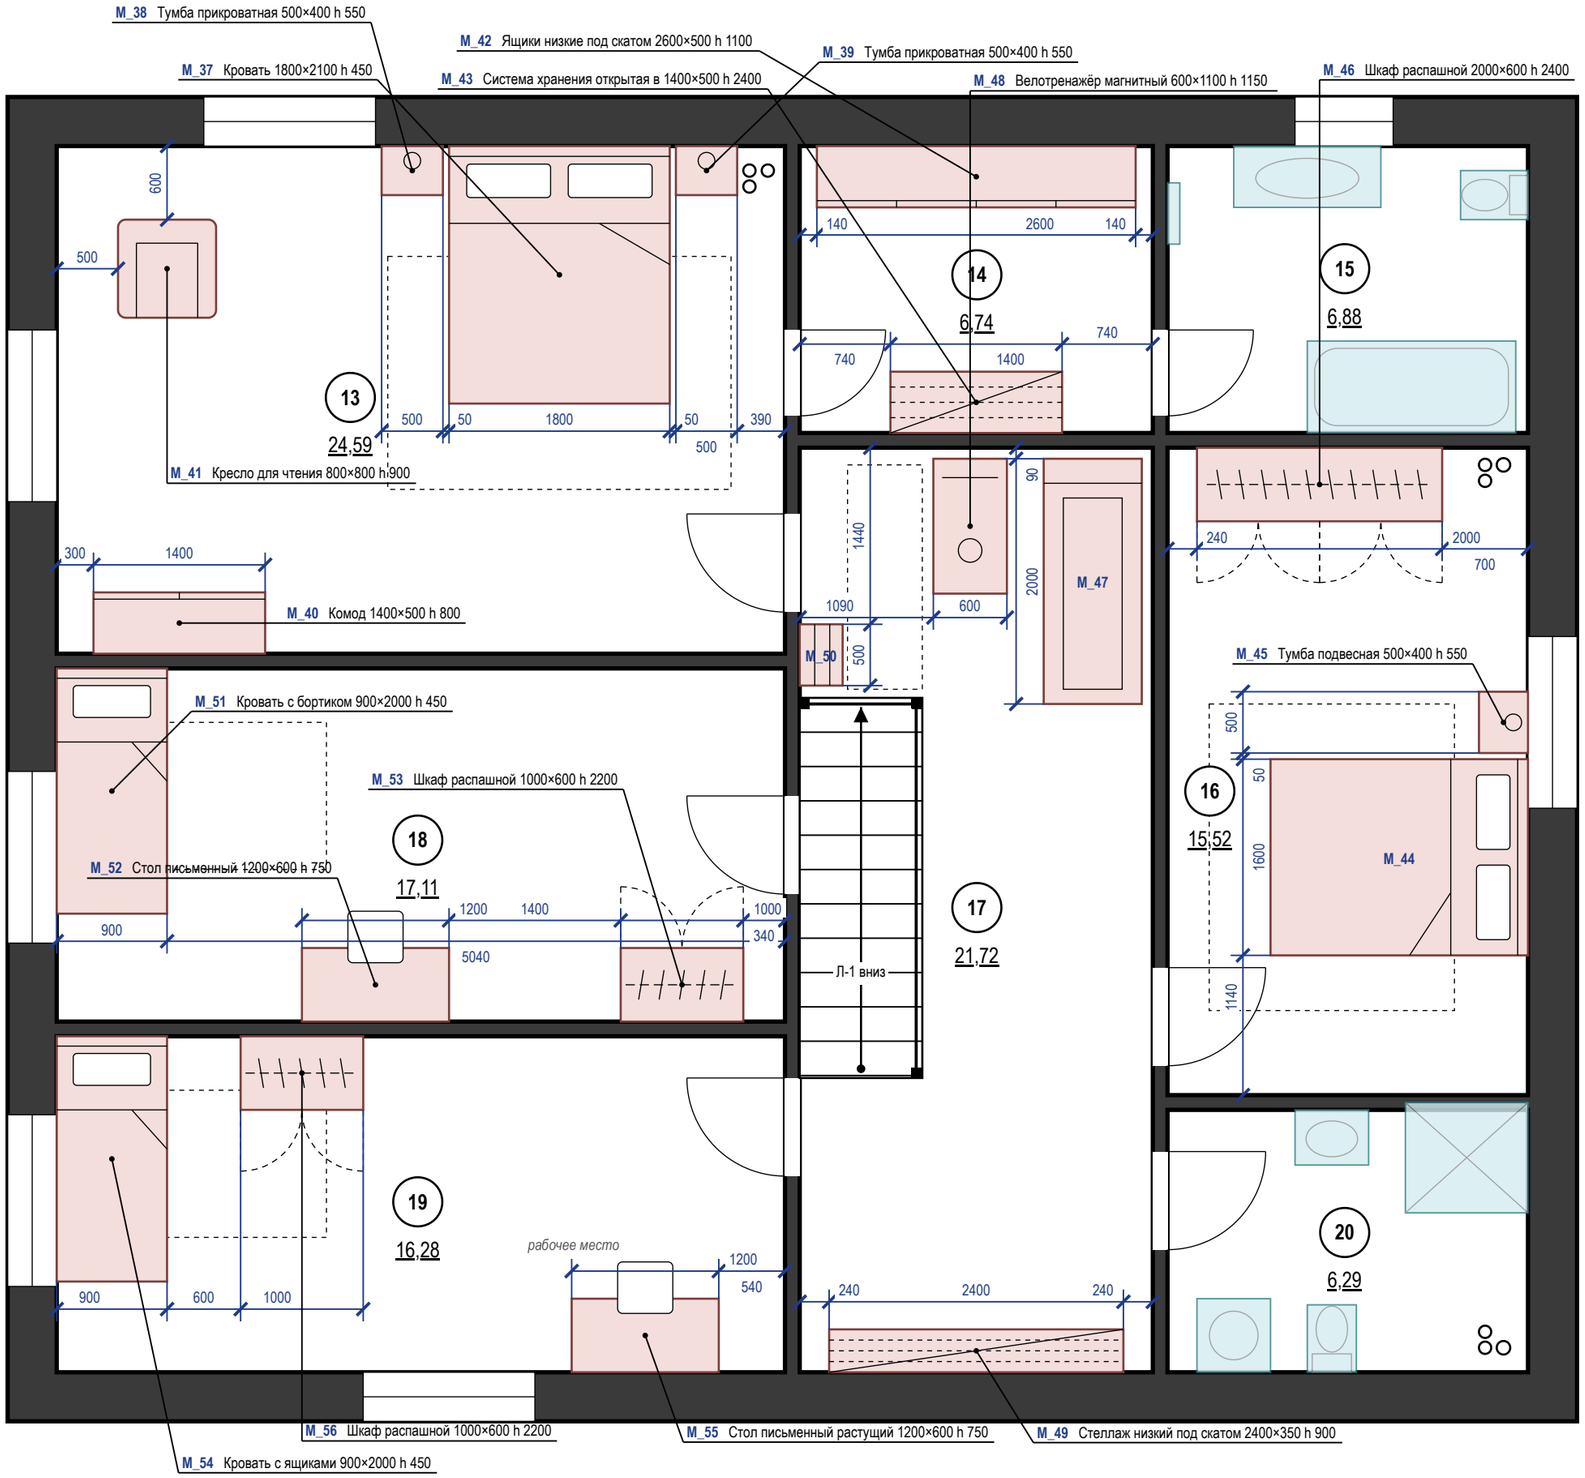

Экспликация помещений

лист обмерного плана · на плане — номера в марках

Ведомость мебели и оборудования

Марка	Наименование	Ш×Г×В, мм	Пом.	Кол.
M_37	Кровать 1800×2000	1800×2100×450	13	1
M_38	Тумба прикроватная	500×400×550	13	1
M_39	Тумба прикроватная	500×400×550	13	1
M_40	Комод	1400×500×800	13	1
M_41	Кресло для чтения	800×800×900	13	1
M_42	Ящики низкие под скатом	2600×500×1100	14	1
M_43	Система хранения открытая в	1400×500×2400	14	1
M_44	Кровать 1600×2000	1600×2100×450	16	1
M_45	Тумба подвесная	500×400×550	16	1
M_46	Шкаф распашной	2000×600×2400	16	1
M_47	Дорожка беговая складная	2000×800×1400	17	1
M_48	Велотренажёр магнитный	600×1100×1150	17	1
M_49	Стеллаж низкий под скатом	2400×350×900	17	1
M_50	Стойка-этажерка для инвентаря	500×350×1000	17	1
M_51	Кровать 900×2000 с бортиком	900×2000×450	18	1
M_52	Стол письменный	1200×600×750	18	1
M_53	Шкаф распашной	1000×600×2200	18	1
M_54	Кровать 900×2000 с ящиками	900×2000×450	19	1
M_55	Стол письменный растущий	1200×600×750	19	1
M_56	Шкаф распашной	1000×600×2200	19	1

Ш — вдоль стены (изголовья), Г — от стены (длина кровати)

Материалы, модели, допуск замены — лист 15

Примечания

1. Размеры — в мм от чистовых поверхностей стен; размеры мебели уточнить после отделочных работ; общие указания — лист 2.
2. Отступ от стены, на плане не образмерен: M_47 — 90 мм, M_48 — 90 мм.

	Лист	№ док.	Подпись	Дата	
Дизайнер	Кырлан А.С.			19.10.26	

Проект: Дом 331 м²

План размещения мебели и оборудования · Мансарда

Стадия	Лист	Листов
П	14	155

выпуск 18.10.2026 № ffc1f29499 · стр. 14 из 155

Поз.	Наименование и техническая характеристика	Тип, марка, обозначение документа, опросного листа	Код продукции	Поставщик	Ед. измерения	Кол.	Масса 1 ед., кг	Примечание
	Мебель встроенная и корпусная (изготовление по чертежам мебельщика)							
M_01	Модуль под мойку у окна; корпус ЛДСП, фасады — матовая эмаль в тон стен; Ш×Г×В 800×600×900 мм			изготовление на заказ	шт.	1		пом. 1
M_02	Посудомоечная машина встроенная; корпус ЛДСП, фасады — матовая эмаль в тон стен; Ш×Г×В 600×600×900 мм			изготовление на заказ	шт.	1		пом. 1
M_03	Модуль с ящиками; корпус ЛДСП, фасады — матовая эмаль в тон стен; Ш×Г×В 400×600×900 мм			изготовление на заказ	шт.	1		пом. 1
M_04	Модуль с варочной панелью и духовым шкафом; корпус ЛДСП, фасады — матовая эмаль в тон стен; Ш×Г×В 800×600×900 мм			изготовление на заказ	шт.	1		пом. 1
M_05	Колонна с холодильником; корпус ЛДСП, фасады — матовая эмаль в тон стен; Ш×Г×В 700×650×2200 мм			изготовление на заказ	шт.	1		пом. 1
M_06	Модуль с ящиками; корпус ЛДСП, фасады — матовая эмаль в тон стен; Ш×Г×В 800×600×900 мм			изготовление на заказ	шт.	1		пом. 1
M_07	Остров с барной консолью из массива дуба, столешница — кварц; корпус ЛДСП, фасады — рейка из массива дуба, столешница — кварцевый агломерат 20 мм, консоль для завтрака — массив дуба 40 мм; Ш×Г×В 2000×900×900 мм			изготовление на заказ	шт.	1		пом. 1
M_09	Навесной шкаф, фасад в тон острова; корпус ЛДСП, фасады — матовая эмаль в тон стен; Ш×Г×В 600×350×900 мм			изготовление на заказ	шт.	1		пом. 1
M_10	Навесной шкаф узкий, полки для специй; корпус ЛДСП, фасады — матовая эмаль в тон стен; Ш×Г×В 400×350×900 мм			изготовление на заказ	шт.	1		пом. 1
M_11	Полки открытые из массива дуба у окна, 3 яруса; полки — массив дуба 30 мм, масло; кронштейны — чёрная сталь; Ш×Г×В 500×350×900 мм			изготовление на заказ	шт.	1		пом. 1
M_12	Пенал-кладовая с выдвижными корзинами; корпус ЛДСП, фасады — матовая эмаль в тон стен; Ш×Г×В 600×600×2200 мм			изготовление на заказ	шт.	1		пом. 1
M_24	Шкаф-купе, светлый дуб; корпус ЛДСП, фасады — матовая эмаль в цвет стен (Farrow & Ball No. 226); Ш×Г×В 1400×600×2600 мм			изготовление на заказ	шт.	1		пом. 8
M_46	Шкаф распашной, фасады — шпон ясеня с вертикальной рейкой; корпус ЛДСП, фасады — шпон ясеня с вертикальной рейкой, масло; Ш×Г×В 2000×600×2400 мм			изготовление на заказ	шт.	1		пом. 16
M_53	Шкаф распашной, фасады — матовая эмаль шалфей; корпус ЛДСП, фасады МДФ — матовая эмаль NCS S 3020-G30Y; Ш×Г×В 1000×600×2200 мм			изготовление на заказ	шт.	1		пом. 18
M_56	Шкаф распашной (вне ската), фасады — дуб и эмаль терракота; корпус ЛДСП, фасады — шпон дуба и МДФ в матовой эмали NCS S 3040-Y70R; Ш×Г×В 1000×600×2200 мм			изготовление на заказ	шт.	1		пом. 19
	Мебель покупная							
M_08	Стол обеденный 2000×1000, массив дуба; шпон, дуб натуральный, матовое масло; Ш×Г×В 2000×1000×750 мм			аналог по характеристикам	шт.	1		пом. 1; замена ≤ габарита
M_57	Стул обеденный к столу M_08; обивка — ткань, цвет Tikkurila V451; каркас — дуб натуральный; Ш×Г×В 450×500×820 мм			аналог по характеристикам	шт.	3		пом. 1; замена ≤ габарита
M_13	Письменный стол у окна, массив дуба на чёрном стальном подстолье; дерево — дуб массив, масло, металл — чёрный матовый; Ш×Г×В 1400×700×750 мм			аналог по характеристикам	шт.	1		пом. 2; замена ≤ габарита
M_14	Кресло рабочее на колёсах, кожа коньячная; обивка кожа натуральная, коньяк; Ш×Г×В 600×600×900 мм			аналог по характеристикам	шт.	1		пом. 2; замена ≤ габарита
M_15	Диван-кровать гостевой, шерстяной твид; обивка шерстяной твид, серо-оливковый меланж; Ш×Г×В 2000×900×850 мм			аналог по характеристикам	шт.	1		пом. 2; замена ≤ габарита
M_16	Стеллаж для книг, чёрная сталь и полки из дуба; каркас — чёрная сталь, полки — массив дуба; Ш×Г×В 1600×400×2200 мм			аналог по характеристикам	шт.	1		пом. 2; крепление к стене; замена ≤ габарита
M_17	Стеллаж технический; каркас и полки — ЛДСП, декор «дуб натуральный»; Ш×Г×В 1200×400×2000 мм			аналог по характеристикам	шт.	1		пом. 4; замена ≤ габарита
M_18	Диван угловой, лён-рогожка; обивка лён-рогожка плотный, молочный; Ш×Г×В 3200×1000×820 мм			аналог по характеристикам	шт.	1		пом. 5; замена ≤ габарита
M_19	Столик журнальный, столешница — сланец, подстолье дуб; столешница — сланец 20 мм, подстолье — массив дуба; Ш×Г×В 1200×700×420 мм			аналог по характеристикам	шт.	1		пом. 5; замена ≤ габарита
M_20	Кресло, букле (овечья шерсть); обивка букле, овечья шерсть, молочный; Ш×Г×В 850×850×850 мм			аналог по характеристикам	шт.	1		пом. 5; замена ≤ габарита
M_21	Кресло-качалка, кожа и ясень; обивка кожа натуральная, тёмный коньяк, дерево — ясень гнутый; Ш×Г×В 850×850×850 мм			аналог по характеристикам	шт.	1		пом. 5; замена ≤ габарита
M_22	Буфет низкий, дуб; шпон, дуб натуральный, матовое масло; Ш×Г×В 1600×450×800 мм			аналог по характеристикам	шт.	1		пом. 5; крепление к стене; замена ≤ габарита
ОБ_01	ТВ-стена с камином, облицовка — колотый сланец; короб ГКЛ с облицовкой колотым сланцем, полка из массива дуба; Ш×Г×В 2400×450×600 мм			аналог по характеристикам	шт.	1		пом. 5; замена ≤ габарита
M_23	Стеллаж для хранения; каркас и полки — ЛДСП, декор «дуб натуральный»; Ш×Г×В 2600×500×2200 мм			аналог по характеристикам	шт.	1		пом. 7; замена ≤ габарита
M_25	Банкетка; Ш×Г×В 1000×400×450 мм			аналог по характеристикам	шт.	1		пом. 8; замена ≤ габарита

Примечания

1. Позиции мебели совпадают с марками на плане расстановки; размеры Ш×Г×В — Ш вдоль стены, Г от стены.
2. Встроенная и корпусная мебель изготавливается по чертежам мебельщика после контрольного обмера; графы «Тип, марка» и «Код продукции» для неё не заполняются (ГОСТ 21.110-2013).
3. Покупные изделия — аналог по характеристикам: заменять только на изделия не больше указанного габарита и того же материала и цвета.
4. Материал и цвет, не указанные в данных изделия, приняты по концепции: тон дерева — по полу, обивка — по вторичному цвету палитры; образцы согласовать до заказа.
5. Масса 1 ед. для изделий до 25 кг не указывается. Техника — по монтажным схемам изготовителя; выводы — по листам ЭОМ и ВК.

					Проект: Дом 331 м²	
	Лист	№ док.	Подпись	Дата	Спецификация мебели и оборудования	Стадия / Лист / Листов
Дизайнер	Кырлан А.С.			19.10.26		П / 15 / 155

Поз.	Наименование и техническая характеристика	Тип, марка, обозначение документа, опросного листа	Код продукции	Поставщик	Ед. измерения	Кол.	Масса 1 ед., кг	Примечание
M_26	Стеллаж для инструмента и шин; каркас и полки — ЛДСП, декор «дуб натуральный»; Ш×Г×В 3000×500×2000 мм			аналог по характеристикам	шт.	1		пом. 10; крепление к стене; замена ≤ габарита
M_27	Силовая стойка со скамьёй и штангой; стальная рама, порошковая окраска, чёрный матовый; под тренажёр — резиновый коврик 10 мм; Ш×Г×В 1200×1500×2300 мм			аналог по характеристикам	шт.	1		пом. 10; замена ≤ габарита
M_28	Верстак с перфопанелью; шпон, дуб натуральный, матовое масло; Ш×Г×В 1800×700×900 мм			аналог по характеристикам	шт.	1		пом. 10; замена ≤ габарита
M_29	Тренажёр гребной магнитный, складной; алюминиевая направляющая, маховик магнитный или водяной, сиденье на роликах; под тренажёр — резиновый коврик 10 мм; Ш×Г×В 2400×600×500 мм			аналог по характеристикам	шт.	1		пом. 10; замена ≤ габарита
M_30	Стойка для гантелей 2 яруса, пары 4–20 кг; стальная рама, порошковая окраска, чёрный матовый; гантели с обрезиненными дисками; Ш×Г×В 1000×500×800 мм			аналог по характеристикам	шт.	1		пом. 10; крепление к стене; замена ≤ габарита
M_31	Стенка шведская, бук, с навесным турником; массив бука, лак матовый; перекладины Ø40 шаг 200; крепление к стене — анкеры по основанию, не менее 6; Ш×Г×В 900×150×2300 мм			аналог по характеристикам	шт.	1		пом. 10; крепление к стене; замена ≤ габарита
M_32	Стол летний; шпон, дуб натуральный, матовое масло; Ш×Г×В 1600×900×750 мм			аналог по характеристикам	шт.	1		пом. 11; замена ≤ габарита
M_33	Диван плетёный; обивка — ткань, цвет Tikkurila V451; Ш×Г×В 2000×800×800 мм			аналог по характеристикам	шт.	1		пом. 11; замена ≤ габарита
M_34, M_35	Кресло плетёное; обивка — ткань, цвет Tikkurila V451; Ш×Г×В 800×800×800 мм			аналог по характеристикам	шт.	2		пом. 11; замена ≤ габарита
M_36	Столик кофейный из тика; шпон, дуб натуральный, матовое масло; Ш×Г×В 1000×600×420 мм			аналог по характеристикам	шт.	1		пом. 11; замена ≤ габарита
M_58	Стул обеденный к столу M_32; обивка — ткань, цвет Tikkurila V451; каркас — дуб натуральный; Ш×Г×В 450×500×820 мм			аналог по характеристикам	шт.	4		пом. 11; замена ≤ габарита
M_37	Кровать 1800×2000, изголовье — мягкое в шерстяном твиде; обивка шерстяной твид, серо-коричневый, дерево — дуб массив, царги и ножки; Ш×Г×В 1800×2100×450 мм			аналог по характеристикам	шт.	1		пом. 13; замена ≤ габарита
M_38, M_39	Тумба прикроватная, массив ореха; дерево — орех массив, масло; Ш×Г×В 500×400×550 мм			аналог по характеристикам	шт.	2		пом. 13; замена ≤ габарита
M_40	Комод, дуб брашированный, фасады с кожаными ручками; дерево — дуб брашированный, масло; Ш×Г×В 1400×500×800 мм			аналог по характеристикам	шт.	1		пом. 13; крепление к стене; замена ≤ габарита
M_41	Кресло для чтения, букле (овечья шерсть); обивка букле, овечья шерсть, молочный; Ш×Г×В 800×800×900 мм			аналог по характеристикам	шт.	1		пом. 13; замена ≤ габарита
M_42	Ящики низкие под скатом (до колена 1200); шпон, дуб натуральный, матовое масло; Ш×Г×В 2600×500×1100 мм			аналог по характеристикам	шт.	1		пом. 14; замена ≤ габарита
M_43	Система хранения открытая в полную высоту (у перегородки, вне ската); каркас и полки — ЛДСП, декор «дуб натуральный»; Ш×Г×В 1400×500×2400 мм			аналог по характеристикам	шт.	1		пом. 14; замена ≤ габарита
M_44	Кровать 1600×2000, изголовье — вертикальная рейка из ясеня; дерево — ясень массив, рейка; Ш×Г×В 1600×2100×450 мм			аналог по характеристикам	шт.	1		пом. 16; замена ≤ габарита
M_45	Тумба подвесная, ясень; дерево — ясень шпон; Ш×Г×В 500×400×550 мм			аналог по характеристикам	шт.	1		пом. 16; крепление к стене; замена ≤ габарита
M_47	Дорожка беговая складная, полотно 1400×500; стальная рама, порошковая окраска, чёрный матовый; под тренажёр резиновый коврик 10 мм; Ш×Г×В 2000×800×1400 мм			аналог по характеристикам	шт.	1		пом. 17; замена ≤ габарита
M_48	Велотренажёр магнитный; стальная рама, порошковая окраска, чёрный матовый; под тренажёр — резиновый коврик 10 мм; Ш×Г×В 600×1100×1150 мм			аналог по характеристикам	шт.	1		пом. 17; замена ≤ габарита
M_49	Стеллаж низкий под скатом для книг и инвентаря; каркас и полки — ЛДСП, декор «дуб натуральный»; Ш×Г×В 2400×350×900 мм			аналог по характеристикам	шт.	1		пом. 17; крепление к стене; замена ≤ габарита
M_50	Стойка-этажерка для инвентаря: гантели 2–8 кг, эспандеры, ролик; стальная рама, порошковая окраска, чёрный матовый; гантели с обрезиненными дисками; Ш×Г×В 500×350×1000 мм			аналог по характеристикам	шт.	1		пом. 17; крепление к стене; замена ≤ габарита
M_51	Кровать 900×2000 с бортиком, массив сосны; дерево — сосна массив, воск; Ш×Г×В 900×2000×450 мм			аналог по характеристикам	шт.	1		пом. 18; замена ≤ габарита
M_52	Стол письменный, столешница ЛДСП светлый ясень, ножки — белая сталь; столешница ЛДСП «светлый ясень», ножки сталь, белая эмаль; Ш×Г×В 1200×600×750 мм			аналог по характеристикам	шт.	1		пом. 18; замена ≤ габарита
M_54	Кровать 900×2000 с ящиками, массив берёзы; дерево — берёза массив, масло; Ш×Г×В 900×2000×450 мм			аналог по характеристикам	шт.	1		пом. 19; замена ≤ габарита
M_55	Стол письменный растущий, берёзовая фанера на регулируемом каркасе; столешница — берёзовая фанера, лак; каркас сталь, тёмно-серая эмаль, регулировка 600–800; Ш×Г×В 1200×600×750 мм			аналог по характеристикам	шт.	1		пом. 19; замена ≤ габарита
	Техника встраиваемая и бытовая, светильники под розетки							
	Посудомоечная машина встраиваемая, в модуле M_02; ниша 600 мм			аналог по характеристикам	шт.	1		пом. 1; по схеме изготовителя
	Варочная панель встраиваемая, электрическая, в модуле M_04			аналог по характеристикам	шт.	1		пом. 1; по схеме изготовителя

					Проект: Дом 331 м²
	Лист	№ док.	Подпись	Дата	Спецификация мебели и оборудования (продолжение)
Дизайнер	Кырлан А.С.			19.10.26	

Стадия	Лист	Листов
П	16	155

Поз.	Наименование и техническая характеристика	Тип, марка, обозначение документа, опросного листа	Код продукции	Поставщик	Ед. измерения	Кол.	Масса 1 ед., кг	Примечание
	Духовой шкаф встраиваемый, в модуле M_04			аналог по характеристикам	шт.	1		пом. 1; по схеме изготовителя
	Холодильник встраиваемый, в модуле M_05			аналог по характеристикам	шт.	1		пом. 1; по схеме изготовителя
	Вытяжка встраиваемая, над модулем M_01			аналог по характеристикам	шт.	1		пом. 1; вывод P21 (ЭОМ)
	Стиральная машина			аналог по характеристикам	шт.	1		пом. 3; вывод P7 (ЭОМ)
	Стиральная машина			аналог по характеристикам	шт.	1		пом. 15; вывод P7 (ЭОМ)
	Стиральная машина, место по листу ВК (ОБ_02); Ш×Г 600×600 мм			аналог по характеристикам	шт.	1		пом. 20; по схеме изготовителя
	Торшер; абажур — ткань или опаловое стекло; лампа 2700 K			аналог по характеристикам	шт.	1		пом. 5; розетка P3 (ЭОМ)
	Торшер, у поз. M_40; абажур — ткань или опаловое стекло; лампа 2700 K			аналог по характеристикам	шт.	1		пом. 13; розетка P5 (ЭОМ)
	Текстиль							
T14	Рулонная штора кассетная, ткань димаут; полиэстер 100 %; цвет NCS S 2005-Y20R; карниз 890 мм, высота 1900 мм			аналог по характеристикам	шт.	1		пом. 1
T7	Портьеры на люверсах, шерстяной твид; лён 100 %; цвет Farrow & Ball No. 40; карниз 1820 мм, высота 2610 мм, сборка 2			аналог по характеристикам	шт.	2		пом. 2
T8	Тюль, льняная сетка; полиэстер 100 %; цвет NCS S 0804-Y30R; карниз 1820 мм, высота 2610 мм, сборка 2,5			аналог по характеристикам	шт.	1		пом. 2
T9	Ковёр джутовый под диваном; шерсть 100 %; цвет Tikkurila X463; 1700×2300 мм			аналог по характеристикам	шт.	1		пом. 2; с подложкой
T10	Подушки на диван, кожа; букле (шерсть 60 %, полиэстер 40 %); цвет NCS S 3010-Y30R			аналог по характеристикам	шт.	3		пом. 2
T11	Подушки на кровать, акцент; хлопковый бархат 100 %; цвет Farrow & Ball No. 298			аналог по характеристикам	шт.	2		пом. 2
T12	Плед на кровать; шерсть мериноса 100 %; цвет Farrow & Ball No. 298			аналог по характеристикам	шт.	1		пом. 2
T1	Портьеры-волна, два полотна; лён 100 %; цвет NCS S 2005-Y20R; карниз 2150 мм, высота 2690 мм, сборка 2			аналог по характеристикам	шт.	2		пом. 5
T2	Тюль-вуаль, одно полотно; полиэстер 100 %; цвет NCS S 0804-Y30R; карниз 2150 мм, высота 2690 мм, сборка 2,5			аналог по характеристикам	шт.	1		пом. 5
T3	Ковёр мягкой группы, шерсть с джутом; шерсть 100 %; цвет Farrow & Ball No. 243; 3600×2400 мм			аналог по характеристикам	шт.	1		пом. 5; с подложкой
T4	Подушки декоративные на диван, лён; лён 100 %; цвет Farrow & Ball No. 226			аналог по характеристикам	шт.	3		пом. 5
T5	Подушки декоративные на диван, акцент; хлопковый бархат 100 %; цвет Farrow & Ball No. 93			аналог по характеристикам	шт.	2		пом. 5
T6	Плед на диван; шерсть мериноса 100 %; цвет Farrow & Ball No. 93			аналог по характеристикам	шт.	1		пом. 5
T40	Покрытие резиновое модульное 500×500×10 мм под спортзону; резиновая крошка SBR с цветными EPDM-вкраплениями, плиты 500×500, 10 мм; цвет Farrow & Ball No. 243; 1500×6300 мм			аналог по характеристикам	шт.	1		пом. 10
T13	Портьеры-волна, шерсть с блэкаут-подкладкой; лён 100 %; цвет Farrow & Ball No. 229; карниз 2500 мм, высота 2610 мм, сборка 2			аналог по характеристикам	шт.	2		пом. 13
T15	Тюль; полиэстер 100 %; цвет Little Greene No. 105; карниз 2500 мм, высота 2610 мм, сборка 2,5			аналог по характеристикам	шт.	1		пом. 13
T16	Ковёр под кроватью, шерсть ручного ткачества; шерсть 80 %, хлопок 20 %; цвет NCS S 2005-Y20R; 2800×1900 мм			аналог по характеристикам	шт.	1		пом. 13; с подложкой
T17	Подушки декоративные на кровать, шерсть-меланж; лён 100 %; цвет NCS S 2005-Y20R			аналог по характеристикам	шт.	3		пом. 13
T18	Подушки на кровать, акцент; хлопковый бархат 100 %; цвет NCS S 7020-G10Y			аналог по характеристикам	шт.	2		пом. 13
T19	Плед на кровать; шерсть мериноса 100 %; цвет NCS S 7020-G10Y			аналог по характеристикам	шт.	1		пом. 13
T20	Портьеры-волна, хлопок-сатин с блэкаут-подкладкой; лён 100 %; цвет Tikkurila X463; карниз 1820 мм, высота 2610 мм, сборка 2			аналог по характеристикам	шт.	2		пом. 16
T21	Тюль, лён-вуаль; полиэстер 100 %; цвет Little Greene No. 105; карниз 1820 мм, высота 2610 мм, сборка 2,5			аналог по характеристикам	шт.	1		пом. 16
T22	Ковёр под кроватью, шерсть с узором ромбы; шерсть 100 %; цвет NCS S 3010-Y30R; 2000×2500 мм			аналог по характеристикам	шт.	1		пом. 16; с подложкой
T23	Подушки декоративные на кровать, хлопок-рогожка; букле (шерсть 60 %, полиэстер 40 %); цвет Tikkurila X463			аналог по характеристикам	шт.	3		пом. 16
T24	Подушки на кровать, акцент; хлопковый бархат 100 %; цвет Farrow & Ball No. 64			аналог по характеристикам	шт.	2		пом. 16
T25	Плед на кровать; шерсть мериноса 100 %; цвет Farrow & Ball No. 64			аналог по характеристикам	шт.	1		пом. 16
T41	Коврик для йоги и растяжки 1830×610×6, TPE, нескользящий; TPE, 6 мм, двухслойный; цвет NCS S 3020-G30Y; 610×1830 мм			аналог по характеристикам	шт.	1		пом. 17
T26	Портьеры на люверсах, хлопок-канвас с блэкаут-подкладкой; лён 100 %; цвет Tikkurila V451; карниз 1820 мм, высота 2610 мм, сборка 2			аналог по характеристикам	шт.	2		пом. 18

Поз.	Наименование и техническая характеристика	Тип, марка, обозначение документа, опросного листа	Код продукции	Поставщик	Ед. измерения	Кол.	Масса 1 ед., кг	Примечание
Т27	Тюль, хлопковая кисея; полиэстер 100 %; цвет NCS S 0804-Y30R; карниз 1820 мм, высота 2610 мм, сборка 2,5			аналог по характеристикам	шт.	1		пом. 18
Т28	Ковёр под кроватью, хлопок, стираемый; шерсть 100 %; цвет NCS S 2005-Y20R; 1600×1200 мм			аналог по характеристикам	шт.	1		пом. 18; с подложкой
Т29	Подушки на кровать, хлопок-вельвет; букле (шерсть 60 %, полиэстер 40 %); цвет Tikkurila V451			аналог по характеристикам	шт.	3		пом. 18
Т30	Подушки на кровать, акцент; хлопковый бархат 100 %; цвет NCS S 3020-G30Y			аналог по характеристикам	шт.	2		пом. 18
Т31	Плед на кровать; шерсть мериноса 100 %; цвет NCS S 3020-G30Y			аналог по характеристикам	шт.	1		пом. 18
Т32	Портьеры-волна, лён-меланж с блэкаут-подкладкой; лён 100 %; цвет NCS S 2005-Y20R; карниз 1820 мм, высота 2610 мм, сборка 2			аналог по характеристикам	шт.	2		пом. 19
Т33	Тюль, лён-вуаль в мелкую клетку; полиэстер 100 %; цвет Farrow & Ball No. 226; карниз 1820 мм, высота 2610 мм, сборка 2,5			аналог по характеристикам	шт.	1		пом. 19
Т34	Ковёр под кроватью, шерсть с узором «горы»; шерсть 100 %; цвет NCS S 3010-Y30R; 1600×1200 мм			аналог по характеристикам	шт.	1		пом. 19; с подложкой
Т35	Подушки на кровать, хлопок-канвас с принтом; букле (шерсть 60 %, полиэстер 40 %); цвет Tikkurila X463			аналог по характеристикам	шт.	3		пом. 19
Т36	Подушки на кровать, акцент; хлопковый бархат 100 %; цвет NCS S 3040-Y70R			аналог по характеристикам	шт.	2		пом. 19
Т37	Плед на кровать; шерсть мериноса 100 %; цвет NCS S 3040-Y70R			аналог по характеристикам	шт.	1		пом. 19
	Декор							
ДК8	Часы настенные Ø400; 400×400 мм; центр на 1550 мм от пола			аналог по характеристикам	шт.	1	2	пом. 1; крепление: дюбель с крюком, 1 точка
ДК9	Хлорофитум хохлатый на подоконнике (отм. +0,800); 300×200 мм; низ на 800 мм от пола			аналог по характеристикам	шт.	1		пом. 1
ДК23	Ваза с тюльпанами на обеденном столе; 200×350 мм; на M_08			аналог по характеристикам	шт.	1		пом. 1
ДК3	Картина над диваном: офорт в паспарту, рама — орех; 1000×700 мм; низ на 1100 мм от пола			аналог по характеристикам	шт.	1	4	пом. 2; крепление к стене
ДК28	Замиокулькас в кашпо Ø350; 350×350 мм			аналог по характеристикам	шт.	1		пом. 2
ДК1	Картина над буфетом: пейзаж, масло, рама — морёный дуб; 1200×900 мм; низ на 1000 мм от пола			аналог по характеристикам	шт.	1	6	пом. 5; крепление: планка на дюбелях, 4 точки
ДК2	Фикус лировидный в кашпо Ø400; 450×450 мм			аналог по характеристикам	шт.	1		пом. 5
ДК21	Оливковое дерево в кашпо Ø450; 450×450 мм			аналог по характеристикам	шт.	1		пом. 5
ДК22	Ваза с живыми цветами на журнальном столе; 200×350 мм; на M_19			аналог по характеристикам	шт.	1		пом. 5
ДК5	Зеркало; рама — чёрный матовый; 800×1800 мм; низ на 550 мм от пола			аналог по характеристикам	шт.	1	18	пом. 8; крепление: анкер, 4 шт.
ДК31	Зеркало 1200×1500 для контроля техники, безопасное (плёнка), без рамы; 1200×1500 мм; низ на 600 мм от пола			аналог по характеристикам	шт.	1	22	пом. 10; крепление: анкер, 4 шт.
ДК24	Гортензия крупнолистная в кадке Ø500; 500×500 мм			аналог по характеристикам	шт.	1		пом. 11
ДК25	Самшит в кадке Ø450; 450×450 мм			аналог по характеристикам	шт.	1		пом. 11
ДК26	Папоротник нефролепис в ящике 600×250; 250×600 мм			аналог по характеристикам	шт.	1		пом. 11
ДК4	Картина над кроватью: акварель, рама — лиственница; 1000×700 мм; низ на 1300 мм от пола			аналог по характеристикам	шт.	1	4	пом. 13; крепление к стене
ДК27	Фикус каучуконосный в кашпо Ø400; 400×400 мм			аналог по характеристикам	шт.	1		пом. 13
ДК6	Картина над кроватью: натюрморт, масло, рама — тонкая латунь; 1000×700 мм; низ на 1300 мм от пола			аналог по характеристикам	шт.	1	4	пом. 16; крепление к стене
ДК7	Зеркало в рост в раме из ясеня; рама — чёрный матовый; 600×1600 мм; низ на 300 мм от пола			аналог по характеристикам	шт.	1	12	пом. 16; крепление: анкер для пустотелых оснований, 4 шт.
ДК30	Монстера в кашпо Ø450 с фитолампой; 450×450 мм			аналог по характеристикам	шт.	1		пом. 17
ДК10	Картина над кроватью: детская иллюстрация, рама — светлый ясень; 600×700 мм; низ на 1100 мм от пола			аналог по характеристикам	шт.	1	4	пом. 18; крепление к стене
ДК11	Зеркало безопасное (плёнка), рама — светлый ясень; рама — чёрный матовый; 500×1600 мм; низ на 300 мм от пола			аналог по характеристикам	шт.	1	12	пом. 18; крепление: анкер для пустотелых оснований, 4 шт.
ДК12	Картина над кроватью: детский принт, рама — белёный дуб; 600×700 мм; низ на 1100 мм от пола			аналог по характеристикам	шт.	1	4	пом. 19; крепление к стене
ДК13	Зеркало круглое Ø600 в кожаном ремне; рама — чёрный матовый; 600×600 мм; низ на 1150 мм от пола			аналог по характеристикам	шт.	1	12	пом. 19; крепление: анкер для пустотелых оснований, 4 шт.

	Лист	№ док.	Подпись	Дата
Дизайнер	Кырлан А.С.			19.10.26

Проект: Дом 331 м²

Спецификация мебели и оборудования (продолжение)

Стадия	Лист	Листов
П	18	155

выпуск 18.10.2026 № ffc1f29499 · стр. 18 из 155

Ведомость изделий

Марка	Наименование	Пом.	Ш×Г×В, мм	Корпус	Фасад	Кромка, мм скр./вид.	Кол.
M_17	Система хранения	4	1200×400×2000	ЛДСП 16	без фасадов; ящики — МДФ 18, эмаль матовая	0,4 / 2	1
M_23	Система хранения	7	2600×500×2200	ЛДСП 16	без фасадов; ящики — МДФ 18, эмаль матовая	0,4 / 2	1
M_24	Шкаф-купе	8	1400×600×2600	ЛДСП 16	рифлёные панели МДФ в алюминиевом профиле	0,4 / 2	1
M_26	Система хранения	10	3000×500×2000	ЛДСП 16	без фасадов; ящики — МДФ 18, эмаль матовая	0,4 / 2	1
M_43	Система хранения	14	1400×500×2400	ЛДСП 16	без фасадов; ящики — МДФ 18, эмаль матовая	0,4 / 2	1
M_46	Шкаф распашной	16	2000×600×2400	ЛДСП 16	МДФ 18, эмаль матовая	0,4 / 2	1
M_49	Система хранения	17	2400×350×900	ЛДСП 16	без фасадов; ящики — МДФ 18, эмаль матовая	0,4 / 2	1
M_53	Шкаф распашной	18	1000×600×2200	ЛДСП 16	МДФ 18, эмаль матовая	0,4 / 2	1
M_56	Шкаф распашной	19	1000×600×2200	ЛДСП 16	МДФ 18, эмаль матовая	0,4 / 2	1
M_06	Модуль нижний: ящики	1	800×600×900	ЛДСП 16	МДФ 18, эмаль матовая	0,4 / 2	1
M_11	Модуль навесной: полки	1	500×350×900	ЛДСП 16	МДФ 18, эмаль матовая	0,4 / 2	1
M_01	Модуль нижний: мойка	1	800×600×900	ЛДСП 16	МДФ 18, эмаль матовая	0,4 / 2	1
M_02	Модуль нижний: ПММ	1	600×600×900	ЛДСП 16	МДФ 18, эмаль матовая	0,4 / 2	1
M_09	Модуль навесной: полки	1	600×350×900	ЛДСП 16	МДФ 18, эмаль матовая	0,4 / 2	1
M_03	Модуль нижний: ящики	1	400×600×900	ЛДСП 16	МДФ 18, эмаль матовая	0,4 / 2	1
M_04	Модуль нижний: духовой шкаф, варочная	1	800×600×900	ЛДСП 16	МДФ 18, эмаль матовая	0,4 / 2	1
M_10	Модуль навесной: полки	1	400×350×900	ЛДСП 16	МДФ 18, эмаль матовая	0,4 / 2	1
M_05	Пенал: холодильник встр.	1	700×650×2200	ЛДСП 16	МДФ 18, эмаль матовая	0,4 / 2	1
M_12	Пенал: полки	1	600×600×2200	ЛДСП 16	МДФ 18, эмаль матовая	0,4 / 2	1

Ведомость встраиваемой техники

Поз.	Прибор	Ниша, вырез, мм	Вентиляция	Питание	Схема
M_01	Мойка врезная / подстольная с сифоном	вырез по шаблону, ориентир 700 × 480		смеситель — выводы ВК	по модели
M_02	Посудомоечная машина встраиваемая, 60 см	ниша 600 × 862 (от пола до низа столешницы)	зазор в цоколе, по схеме	розетка в соседнем модуле	по модели
M_04	Духовой шкаф встраиваемый, 60 см	ниша 560 × 595, глубина ≥ 550	зазор за шкафом, вырез в задней стенке	вывод кабеля под шкафом	по модели
M_04	Варочная панель индукционная, 60 см	вырез в столешнице 560 × 490		вывод кабеля под модулем	по модели
M_05	Холодильник встраиваемый, ниша 1780	ниша 1780 × 560 × 550	решётка в цоколе, канал за корпусом, выход сверху	розетка над нишей или в соседнем модуле	по модели
M_04	Вытяжка настенная, 60 см	низ ≥ 650 над панелью	воздуховод к вентканалу, короб до потолка	вывод кабеля в коробе	по модели

Ведомость фурнитуры


№	Фурнитура	Тип, размер	Изделия	Кол.
1	Штанга выдвижная торцевая	L по глубине	M_17, M_23, M_26, M_43, M_49	9
2	Полкодержатель с фиксацией	ø5 мм	M_17, M_23, M_24, M_26, M_43, M_46, M_49, M_53, M_56, M_11, M_09, M_10, M_05, M_12	220
3	Опора регулируемая с цоколем на клипсах	ход 20 мм	M_17, M_23, M_24, M_26, M_43, M_46, M_49, M_53, M_56	66
4	Анкер по основанию стены	по таблице крепежа	M_17, M_23, M_24, M_26, M_43, M_46, M_49, M_53, M_56, M_11, M_09, M_10	75
5	Уголок крепления к стене от опрокидывания	стальной	M_17, M_23, M_24, M_26, M_43, M_46, M_49, M_53, M_56, M_05, M_12	22
6	Система дверей купе: профиль, направляющие, ролики	на 2 двери	M_24	1
7	Ручка-профиль вертикальная	в цвет профиля	M_24	2
8	Штанга овальная 30×15, L = 676	+ 2 держателя	M_24	1
9	Полка для обуви выдвижная наклонная	ширина 676	M_24	3
10	Петля накладная 110° с доводчиком	чашка 35 мм	M_46, M_53, M_56, M_11, M_01, M_09, M_10, M_05, M_12	72
11	Штанга овальная 30×15, L = 976	+ 2 держателя	M_46	1
12	Штанга овальная 30×15, L = 968	+ 2 держателя	M_53, M_56	2
13	Направляющие полного выдвижения с доводчиком NL 500	пара	M_06, M_03, M_04	7
14	Ручка-профиль	латунь матовая	M_06, M_11, M_01, M_02, M_09, M_03, M_04, M_10, M_05, M_12	19
15	Опора кухонная регулируемая 100–120 мм	+ клипса цоколя	M_06, M_01, M_02, M_03, M_04, M_05, M_12	36
16	Навес регулируемый для навесного шкафа	пара на секцию	M_11, M_09, M_10	3
17	Шина монтажная	L = 440	M_11	1
18	Комплект навески фасада ПММ	из поставки машины	M_02	1
19	Шина монтажная	L = 540	M_09	1
20	Шина монтажная	L = 340	M_10	1

Примечания


1. Модели техники выбирает заказчик до изготовления мебели; ниши, вырезы и вентиляция — по монтажной схеме выбранной модели (условие гарантии), её номер вносится в ведомость.
2. Количество фурнитуры — по чертежам изделий; запас крепежа 5 %. Аналоги — по характеристикам (доводчик, нагрузка, ход).
3. Цвет корпусов, фасадов и профилей — по колерной карте проекта.

					Проект: Дом 331 м²			
	Лист	№ док.	Подпись	Дата	Ведомости изделий, техники и фурнитуры	Стадия	Лист	Листов
Дизайнер	Кырлан А.С.			19.10.26		П	19	155

Фрагмент 1. Санузел 1 этажа (пом. 3)

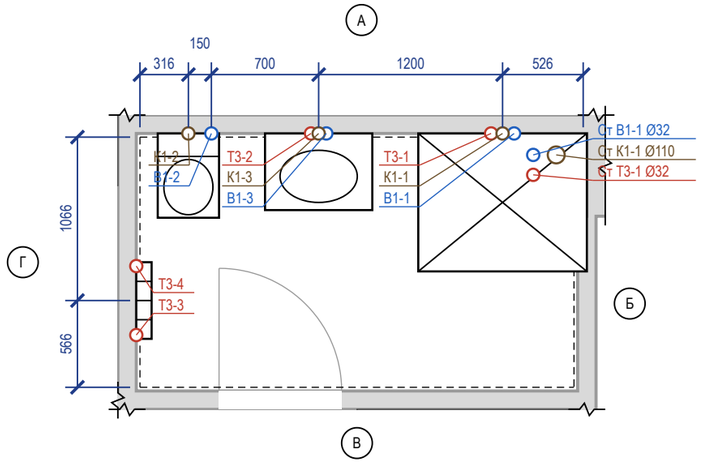

Фрагмент 2. Кухня-столовая (пом. 1)

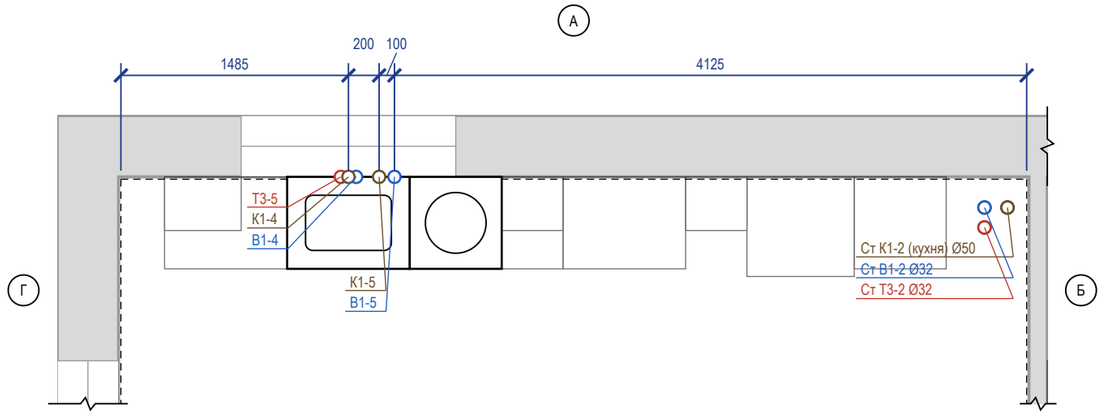

Ведомость привязок выводов

Код	Прибор	Ø	H, мм	Привязка от чист. стен, мм	Прим.
В1-1	С_01 душ	½"	1200	ст. А: 451 от Б	межос. 150
Т3-1	С_01 душ	½"	1200	ст. А: 601 от Б	межос. 150
К1-1	С_01 душ	Ø50	70	ст. А: 526 от Б	сифон поддона
В1-2	С_02 унитаз подвесной	½"	250	ст. А: 466 от Г	в раме инсталляции
К1-2	С_02 унитаз подвесной	Ø110	220	ст. А: 316 от Г	
В1-3	С_03 умывальник	½"	600	ст. А: 1216 от Г	межос. 100
Т3-2	С_03 умывальник	½"	600	ст. А: 1116 от Г	межос. 100
К1-3	С_03 умывальник	Ø50	500	ст. А: 1166 от Г	
Т3-3	С_04 полотенцесушитель	½"	1150	ст. Г: 341 от В	подача, межос. 450; байпас и краны
Т3-4	С_04 полотенцесушитель	½"	1150	ст. Г: 791 от В	обратка
В1-4	П5 мойка кухонная	½"	600	ст. А: 1535 от Г	межос. 100
Т3-5	П5 мойка кухонная	½"	600	ст. А: 1435 от Г	межос. 100
К1-4	П5 мойка кухонная	Ø50	400	ст. А: 1485 от Г	
В1-5	П6 посудомоечная машина	½"	550	ст. А: 1785 от Г	кран ПММ в шкафу мойки
К1-5	П6 посудомоечная машина	Ø40	550	ст. А: 1685 от Г	слив ПММ в шкафу мойки

Условные обозначения

- вывод В1 (код — в ведомости привязок)
- вывод Т3 (код — в ведомости привязок)
- вывод К1 (код — в ведомости привязок)
- сантехприбор по расстановке (габарит модели)
- чистовая поверхность стены (от неё привязки)
- стояк «Ст К1-N / Ст В1-N» (ГОСТ 21.601), Ø мм
- линия обрыва (граница фрагмента)
- А — обозначение стены А–Г (как на развёртках)


Примечания

1. Привязки выводов даны от чистовых поверхностей стен (облицовка на сторону: санузел 1 этажа — 24 мм (штукатурка 10 + клей 5 + плитка 9); кухня-столовая — 22 мм (фартук: штукатурка 10 + клей 3 + плитка 9)); эти же грани — на развёртках и в раскладке плитки. Высоты — от чистого пола помещения.
2. До черновой разводки сверить по паспорту выбранного прибора (смеситель, инсталляция, сифон).
3. Горячая вода (Т3) — слева от холодной (В1), если смотреть на прибор. Допуск установки выводов: ±5 мм в группе, ±20 мм у отдельно стоящих.
4. Расчёт систем водоснабжения и канализации и подбор оборудования выполняет проектная организация; лист задаёт места и высоты выводов.
5. Посудомоечная машина П6: кран и слив — отдельными выводами в шкафу мойки (не за машиной), до машины ≤ 1500 мм.
6. Прибор П5 мойка кухонная, П6 посудомоечная машина взят из расстановки мебели (по шкафу с мойкой).
7. Стояки в коробах/шахтах не замоноличивать; стояк К1 в коробе — звукоизоляция стояка в коробе без жёсткого контакта с трубой; к арматуре и ревизиям — люк не меньше 300×400.


					Проект: Дом 331 м²
	Лист	№ док.	Подпись	Дата	План выводов сантехники · 1-й этаж
Дизайнер	Кырлан А.С.			19.10.26	

Стадия	Лист	Листов
П	20	155

Фрагмент 1. Санузел мастер (пом. 15)

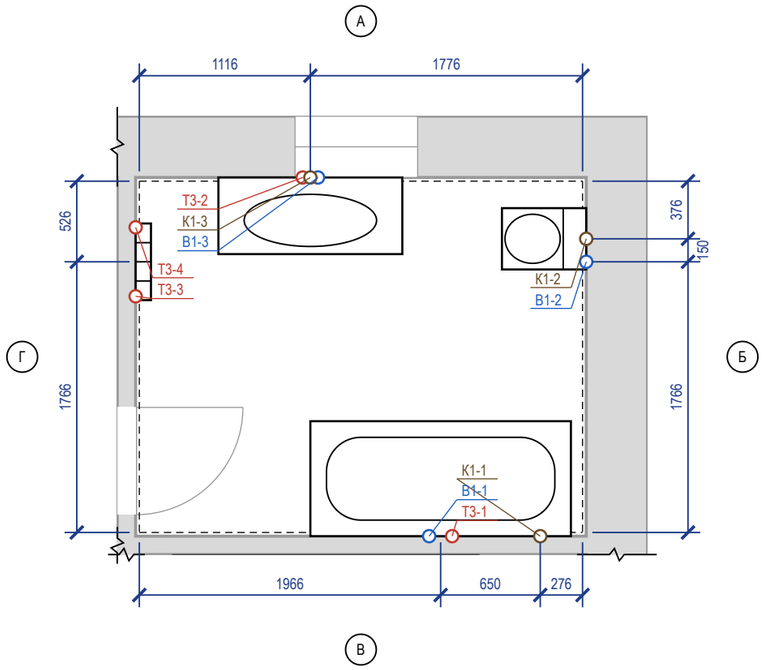

Фрагмент 2. Санузел 2 (пом. 20)

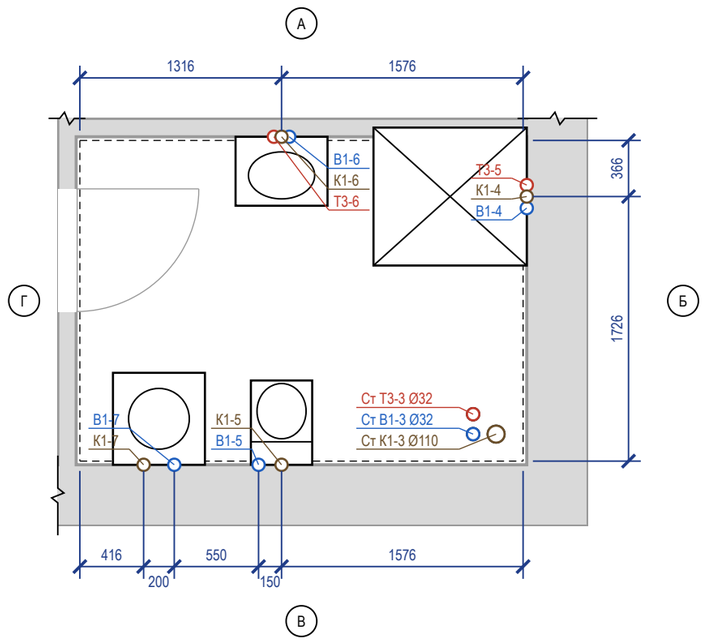

Ведомость привязок выводов

Код	Прибор	Ø	H, мм	Привязка от чист. стен, мм	Прим.
В1-1	С_05 ванна	½"	800	ст. В: 1001 от Б	межос. 150
Т3-1	С_05 ванна	½"	800	ст. В: 851 от Б	межос. 150
К1-1	С_05 ванна	Ø50	50	ст. В: 276 от Б	
В1-2	С_06 унитаз подвесной	½"	250	ст. Б: 526 от А	в раме инсталляции
К1-2	С_06 унитаз подвесной	Ø110	220	ст. Б: 376 от А	
В1-3	С_07 умывальник	½"	600	ст. А: 1166 от Г	межос. 100
Т3-2	С_07 умывальник	½"	600	ст. А: 1066 от Г	межос. 100
К1-3	С_07 умывальник	Ø50	500	ст. А: 1116 от Г	
Т3-3	С_08 полотенцесушитель	½"	1150	ст. Г: 751 от А	подача, межос. 450; байпас и краны
Т3-4	С_08 полотенцесушитель	½"	1150	ст. Г: 301 от А	обратка
В1-4	С_09 душ	½"	1200	ст. Б: 441 от А	межос. 150
Т3-5	С_09 душ	½"	1200	ст. Б: 291 от А	межос. 150
К1-4	С_09 душ	Ø50	70	ст. Б: 366 от А	сифон поддона
В1-5	С_10 унитаз подвесной	½"	250	ст. В: 1166 от Г	в раме инсталляции
К1-5	С_10 унитаз подвесной	Ø110	220	ст. В: 1316 от Г	
В1-6	С_11 умывальник	½"	600	ст. А: 1366 от Г	межос. 100
Т3-6	С_11 умывальник	½"	600	ст. А: 1266 от Г	межос. 100
К1-6	С_11 умывальник	Ø50	500	ст. А: 1316 от Г	
В1-7	ОБ_02 стиральная машина	½"	600	ст. В: 616 от Г	кран машины
К1-7	ОБ_02 стиральная машина	Ø50	600	ст. В: 416 от Г	

Условные обозначения

- вывод В1 (код — в ведомости привязок)
- вывод Т3 (код — в ведомости привязок)
- вывод К1 (код — в ведомости привязок)
- сантехприбор по расстановке (габарит модели)
- чистовая поверхность стены (от неё привязки)
- стояк «Ст К1-N / Ст В1-N» (ГОСТ 21.601), Ø мм
- линия обрыва (граница фрагмента)
- А — обозначение стены А–Г (как на развёртках)


Примечания

1. Привязки выводов даны от чистовых поверхностей стен (облицовка на сторону: санузел мастер — 24 мм (штукатурка 10 + клей 5 + плитка 9); санузел 2 24 мм (штукатурка 10 + клей 5 + плитка 9)); эти же грани — на развёртках и в раскладке плитки. Высоты — от чистого пола помещения.
2. До черновой разводки сверить по паспорту выбранного прибора (смеситель, инсталляция, сифон).
3. Горячая вода (Т3) — слева от холодной (В1), если смотреть на прибор. Допуск установки выводов: ±5 мм в группе, ±20 мм у отдельно стоящих.
4. Расчёт систем водоснабжения и канализации и подбор оборудования выполняет проектная организация; лист задаёт места и высоты выводов.
5. Стояки в коробах/шахтах не замоноличивать; стояк К1 в коробе — звукоизоляция стояка в коробе без жёсткого контакта с трубой; к арматуре и ревизиям — люк не меньше 300×400.


					Проект: Дом 331 м²
	Лист	№ док.	Подпись	Дата	
Дизайнер	Кырлан А.С.			19.10.26	План выводов сантехники · Мансарда

Стадия	Лист	Листов
П	21	155


План квартиры (М 1:400)

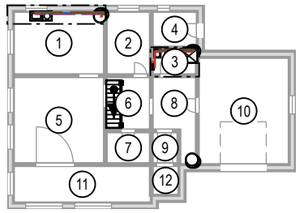

Фр. 1. Санузел 1 этажа (М 1:25)

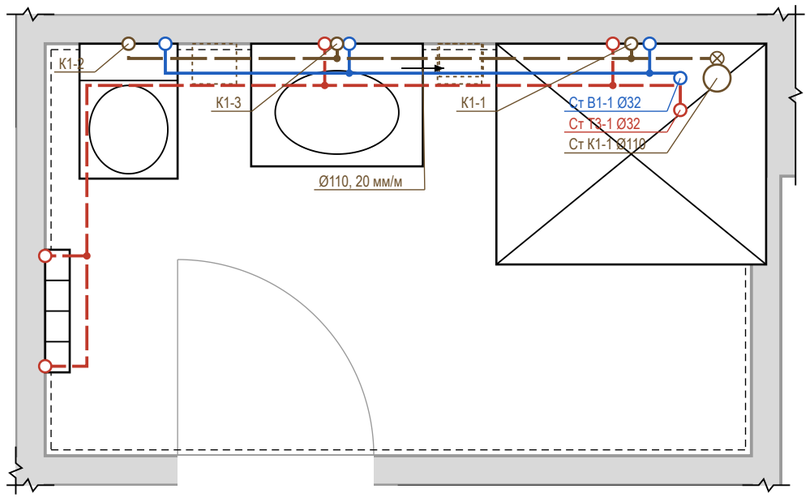

Фр. 2. Кухня-столовая (М 1:25)

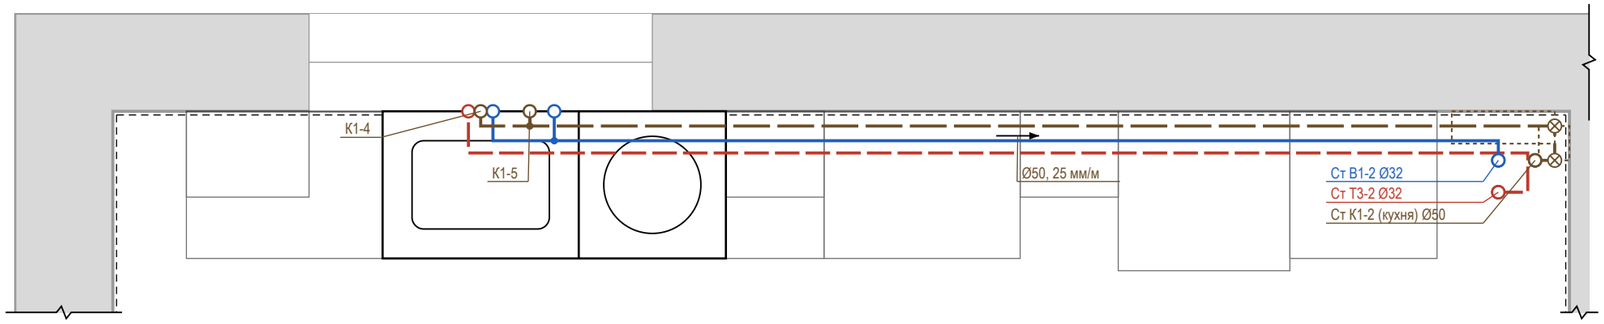

Условные обозначения


- В1 — водопровод хозяйственно-питьевой (ХВС), PP-R Ø20
- Т3 — горячее водоснабжение, подача (ГВС), PP-R Ø20
- К1 — канализация бытовая
- направление уклона К1 / пола: Ø, мм на 1 м
- ревизия (прочистка) К1 — доступ сохранить
- тройник (ответвление к прибору)
- короб К1 над чистым полом (ГКЛВ под плитку)
- вывод В1 (код — в ведомости привязок)
- вывод Т3 (код — в ведомости привязок)
- вывод К1 (код — в ведомости привязок)
- сантехприбор по расстановке (габарит модели)
- стояк «Ст К1-N / Ст В1-N» (ГОСТ 21.601), Ø мм
- линия обрыва (граница фрагмента)
- граница фрагмента на плане (Фр. N)

Профиль выпусков К1 (до врезки в стояк)

Выпуск	Прибор	Ø	L, м	i, мм/м	Δh, мм	Прокладка, мм
К1-2	С_02 унитаз подвесной	Ø110	2,54	20	51	короб 200×140
К1-4	П5 мойка кухонная	Ø50	4,66	25	117	короб 200×110
К1-3	С_03 умывальник	Ø50	1,69	25	42	короб 130×110
К1-1	С_01 душ	Ø50	0,49	25	12	над полом за приборами
К1-5	П6 посудомоечная машина	Ø40	4,46	30	134	короб 210×110

Короб h×b: h — от чистого пола, b — от чистовой стены. Стяжка 35 мм — лист полов.

Узел ввода В1, Т3 (схема, без масштаба)

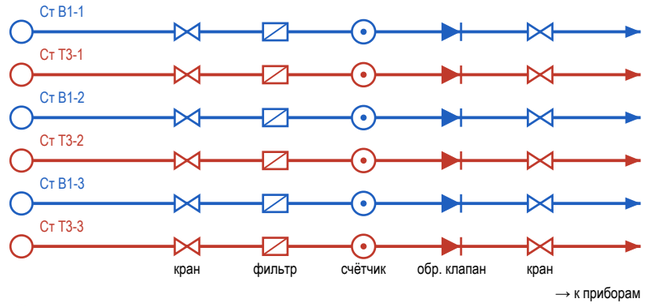

⊗ Ст К1-1, Ст К1-2 (кухня), Ст К1-3: ревизия на стояке — люк в коробе


Примечания

1. Трассы принципиальные, построены от стояков вдоль стен помещений; фактическое положение фиксируется исполнительной схемой с привязками (фото с рулеткой) до закрытия.
2. Уклон К1 не менее 1/d и не более 150 мм/м (СП 30.13330.2020, п. 19.1), приняты практические уклоны; поворот — двумя отводами 45°, ревизия после поворота, доступ сохранить. Стояк К1 в коробе — звукоизоляция стояка в коробе, без жёсткого контакта короба с трубой.
3. Решение по К1: стяжка 35 мм не укрывает трубы (нужно Ø + Δh + 45 мм) — выпуски идут над чистым полом вдоль стен: К1-1 — за приборами и в раме инсталляции; К1-2, К1-4, К1-3, К1-5 — в коробе ГКЛВ под плитку (размеры в профиле). Короба — на развёртках; отметку низа врезки в стояк замерить до черновых работ.
4. На каждом вводе В1 и Т3 — кран шаровой, фильтр, счётчик, обратный клапан; доступ через люк не меньше 300×400. Водопровод — в штробе стен или в коробах; трубы испытать давлением до закрытия (акт скрытых работ).
5. Расчёт систем, диаметры магистралей и подбор оборудования выполняет проектная организация; врезка и перенос стояков — по согласованию с управляющей организацией. Арматуру и привязки сверить по паспортам приборов.


					Проект: Дом 331 м²
	Лист	№ док.	Подпись	Дата	Схема разводки водопровода и канализации · 1-й этаж
Дизайнер	Кырлан А.С.			19.10.26	

Стадия	Лист	Листов
П	22	155


План квартиры (М 1:200)

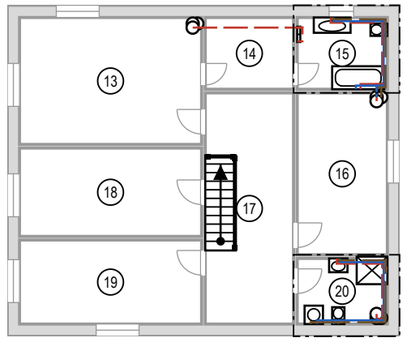

Фр. 1. Санузел мастер (М 1:40)

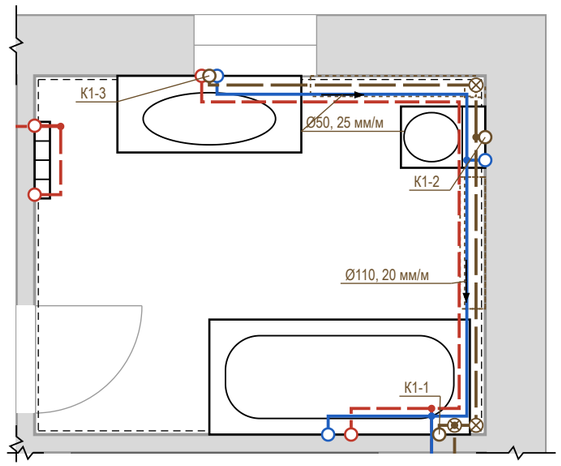

Фр. 2. Санузел 2 (М 1:40)

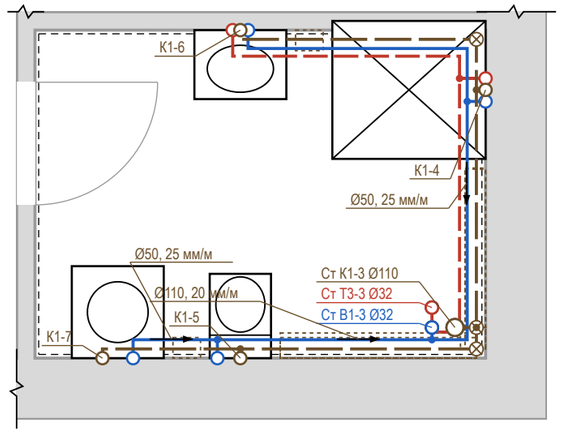

Условные обозначения


- В1 — водопровод хозяйственно-питьевой (ХВС), PP-R Ø20
- Т3 — горячее водоснабжение, подача (ГВС), PP-R Ø20
- К1 — канализация бытовая
- направление уклона К1 / пола: Ø, мм на 1 м
- ⊗ ревизия (прочистка) К1 — доступ сохранить
- • тройник (ответвление к прибору)
- короб К1 над чистым полом (ГКЛВ под плитку)
- ○ вывод В1 (код — в ведомости привязок)
- ○ вывод Т3 (код — в ведомости привязок)
- ○ вывод К1 (код — в ведомости привязок)
- сантехприбор по расстановке (габарит модели)
- ◯ стояк «Ст К1-N / Ст В1-N» (ГОСТ 21.601), Ø мм
- линия обрыва (граница фрагмента)
- граница фрагмента на плане (Фр. N)

Профиль выпусков К1 (до врезки в стояк)

Выпуск	Прибор	Ø	L, м	i, мм/м	Δh, мм	Прокладка, мм
К1-2	С_06 унитаз подвесной	Ø110	2,40	20	48	короб 190×140
К1-5	С_10 унитаз подвесной	Ø110	1,88	20	38	короб 180×140
К1-3	С_07 умывальник	Ø50	4,48	25	112	короб 200×110
К1-6	С_11 умывальник	Ø50	3,62	25	91	короб 180×110
К1-7	ОБ_02 стиральная машина	Ø50	2,78	25	70	короб 150×110
К1-4	С_09 душ	Ø50	1,75	25	44	короб 130×110
К1-1	С_05 ванна	Ø50	0,48	25	12	над полом за приборами

Короб h×b: h — от чистого пола, b — от чистовой стены. Стяжка 35 мм — лист полов.

Узел ввода В1, Т3 (схема, без масштаба)

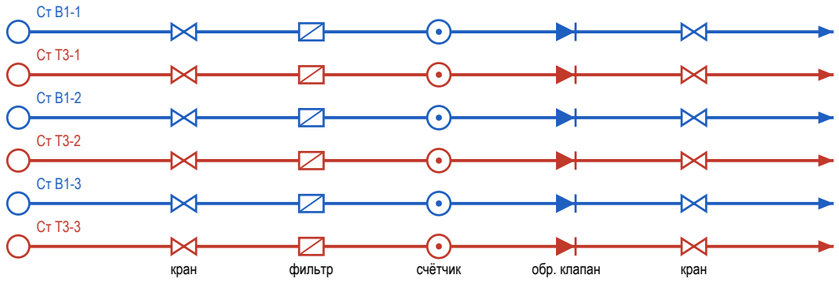

⊗ Ст К1-1, Ст К1-2 (кухня), Ст К1-3: ревизия на стояке — люк в коробе

Примечания

1. Трассы принципиальные, построены от стояков вдоль стен помещений; фактическое положение фиксируется исполнительной схемой с привязками (фото с рулеткой) до закрытия.
2. Уклон К1 не менее 1/d и не более 150 мм/м (СП 30.13330.2020, п. 19.1), приняты практические уклоны; поворот — двумя отводами 45°, ревизия после поворота, доступ сохранить. Стояк К1 в коробе — звукоизоляция стояка в коробе, без жёсткого контакта короба с трубой.
3. Решение по К1: стяжка 35 мм не укрывает трубы (нужно Ø + Δh + 45 мм) — выпуски идут над чистым полом вдоль стен: К1-1 — за приборами и в раме инсталляции; К1-2, К1-5, К1-3, К1-6, К1-7, К1-4 — в коробе ГКЛВ под плитку (размеры в профиле). Короба — на развёртках; отметку низа врезки в стояк замерить до черновых работ.
4. На каждом вводе В1 и Т3 — кран шаровой, фильтр, счётчик, обратный клапан; доступ через люк не меньше 300×400. Водопровод — в штробе стен или в коробах; трубы испытать давлением до закрытия (акт скрытых работ).
5. Расчёт систем, диаметры магистралей и подбор оборудования выполняет проектная организация; врезка и перенос стояков — по согласованию с управляющей организацией. Арматуру и привязки сверить по паспортам приборов.

					Проект: Дом 331 м²
	Лист	№ док.	Подпись	Дата	Схема разводки водопровода и канализации · Мансарда
Дизайнер	Кырлан А.С.			19.10.26	Стадия: П; Лист: 23; Листов: 155


Поз.	Наименование и техническая характеристика	Тип, марка, обозначение документа	Код продукции	Поставщик	Ед. изм.	Кол.	Масса 1 ед., кг	Примечание
	Санитарные приборы							
1	Ванна акриловая 1700×750 мм, с каркасом, экраном и отверстием слив-перелив	аналог		выбор заказчика	шт	1		С_05
2	Унитаз подвесной безободковый, с сиденьем микролифт, крепёж и звукоизолирующая прокладка	Jacob Delafon Struktura EDF102-00		выбор заказчика	шт	3		С_02, С_06, С_10
3	Инсталляция для подвесного унитаза: рама высотой 1120 мм, бачок, клавиша смыва (ось клавиши 1050 мм от чистого пола)	аналог		выбор заказчика	шт	3		С_02, С_06, С_10; короб ГКЛВ
4	Умывальник подвесной 700×500 мм, с отверстием под смеситель и переливом	аналог		выбор заказчика	шт	1		С_03
5	Умывальник подвесной 1200×500 мм, с отверстием под смеситель и переливом	аналог		выбор заказчика	шт	1		С_07
6	Умывальник подвесной 600×450 мм, с отверстием под смеситель и переливом	аналог		выбор заказчика	шт	1		С_11
7	Поддон душевой низкий 1100×900 мм, с сифоном и выпуском Ø50, на ножках/подиуме	аналог		выбор заказчика	шт	1		С_01
8	Поддон душевой низкий 900×1000 мм, с сифоном и выпуском Ø50, на ножках/подиуме	аналог		выбор заказчика	шт	1		С_09
9	Мойка кухонная 800×600 мм, с переливом	аналог		с кухонной мебелью	шт	1		П13
10	Полотенцесушитель водяной (ГВС), с байпасом и кранами	аналог		выбор заказчика	шт	2		С_04, С_08
	Смесители, сифоны и арматура приборов							
11	Смеситель для ванны настенный однорычажный, межосевое 150 мм, с душевым набором (лейка, шланг, держатель)	аналог		выбор заказчика	шт	1		С_05
12	Смеситель для умывальника однорычажный, с донным клапаном	аналог		выбор заказчика	шт	3		С_03, С_07, С_11
13	Душевая система скрытого монтажа с термостатом: встраиваемая часть, верхний душ, ручная лейка	аналог		выбор заказчика	шт	2		С_01, С_09; встраиваемая часть — до плитки
14	Смеситель кухонный однорычажный, высокий излив	аналог		выбор заказчика	шт	1		П13
15	Обвязка ванны слив-перелив Ø40/50 с сифоном	аналог		выбор заказчика	шт	1		С_05
16	Сифон для умывальника бутылочный Ø32/40–50, с гофрой к выпуску	аналог		выбор заказчика	шт	3		С_03, С_07, С_11
17	Сифон для мойки с отводом для ПММ Ø40/50	аналог		выбор заказчика	шт	1		П13
18	Сифон для стиральной машины встраиваемый в стену Ø50, с обратным клапаном	аналог		выбор заказчика	шт	1		ОБ_02
19	Кран угловой ½"×½" с гибкой подводкой 40 см (умывальники, мойка)	аналог		выбор заказчика	шт	8		по 2 на прибор
20	Кран шаровой угловой ½"×¾" для подключения стиральной и посудомоечной машины	аналог		выбор заказчика	шт	2		ОБ_02, П14
21	Узел подключения полотенцесушителя: байпас Ду20, краны шаровые ½" ×2	аналог		выбор заказчика	шт	2		
	Трубопроводы							
22	Труба полипропиленовая PP-R PN20 Ø20×3,4 (В1)	ГОСТ 32415-2013		выбор заказчика	м	28,5	0,17	18,3 + 7,5 + 10 %
23	Труба PP-R, армированная стекловолокном, PN20 Ø20×2,8 (Т3)	ГОСТ 32415-2013		выбор заказчика	м	36	0,15	22,5 + 10,2 + 10 %
24	Труба канализационная ПП Ø40 (К1)	ГОСТ 32414-2013		выбор заказчика	м	1		0,1 + 0,6 + 10 %
25	Труба канализационная ПП Ø50 (К1)	ГОСТ 32414-2013		выбор заказчика	м	16		11,6 + 2,7 + 10 %
26	Труба канализационная ПП Ø110 (К1)	ГОСТ 32414-2013		выбор заказчика	м	8,5		6,7 + 0,7 + 10 %
	Фасонные части и выводы							
27	Отвод канализационный ПП 45° Ø50	ГОСТ 32414-2013		выбор заказчика	шт	18		2 шт. на поворот
28	Отвод канализационный ПП 45° Ø110	ГОСТ 32414-2013		выбор заказчика	шт	16		2 шт. на поворот
29	Тройник канализационный ПП 45° (врезки ветвей)	ГОСТ 32414-2013		выбор заказчика	шт	11		
30	Ревизия канализационная ПП (после поворота трассы)	ГОСТ 32414-2013		выбор заказчика	шт	9		доступ сохранить
31	Фитинги PP-R Ø20: тройники, угольники 90° (ветви и повороты В1, Т3)	ГОСТ 32415-2013		выбор заказчика	шт	51		
32	Водорозетка PP-R Ø20×½" настенная, с креплением	ГОСТ 32415-2013		выбор заказчика	шт	23		коды — лист выводов
	Узлы ввода, люки, короба							
33	Кран шаровой латунный Ду15 PN16 (отключение ввода)	аналог		выбор заказчика	шт	6		Ст В1-1, Ст Т3-1, Ст В1-2, Ст Т3-2, Ст В1-3, Ст Т3-3
34	Фильтр сетчатый косой Ду15	аналог		выбор заказчика	шт	6		
35	Счётчик воды крыльчатый Ду15 (ХВ, ГВ), с поверкой	аналог		выбор заказчика	шт	6		пломба УК
36	Клапан обратный Ду15	аналог		выбор заказчика	шт	6		
37	Люк ревизионный нажимной под плитку 300×400 мм	аналог		выбор заказчика	шт	3		к стоякам и арматуре
38	Звукоизоляция стояка К1 в коробе: рулонный звукоизоляционный материал ≥ 10 мм, обмотка стояка на высоту этажа	аналог		выбор заказчика	м	8,4		Ст К1-1, Ст К1-2 (кухня), Ст К1-3
39	Короб К1 над полом: профиль ПН/ПС, ГКЛВ 12,5 мм под плитку	аналог		выбор заказчика	м	11,6		сечение — лист разводки

Примечания

1. Форма 1 ГОСТ 21.110-2013, ширины граф изменены по п. 4.1. «Аналог» — аналог по характеристикам: модели внести до черновых работ, привязки выводов сверить по паспортам.
2. Бытовая техника не входит (показана арматура подключения), мойка — в комплекте кухни. Длины труб — трасса листа разводки + подъёмы + 10 %.
3. Стояк К1 в коробе — звукоизоляция стояка в коробе без жёсткого контакта короба с трубой.
4. Расчёт систем водоснабжения и канализации, диаметры магистралей и подбор оборудования выполняет проектная организация.

					Проект: Дом 331 м²		
	Лист	№ док.	Подпись	Дата	Спецификация сантехнического оборудования	Стадия	Лист	Листов
Дизайнер	Кырлан А.С.			19.10.26		П	24	155

выпуск 18.10.2026 № ffc1f29499 · стр. 24 из 155

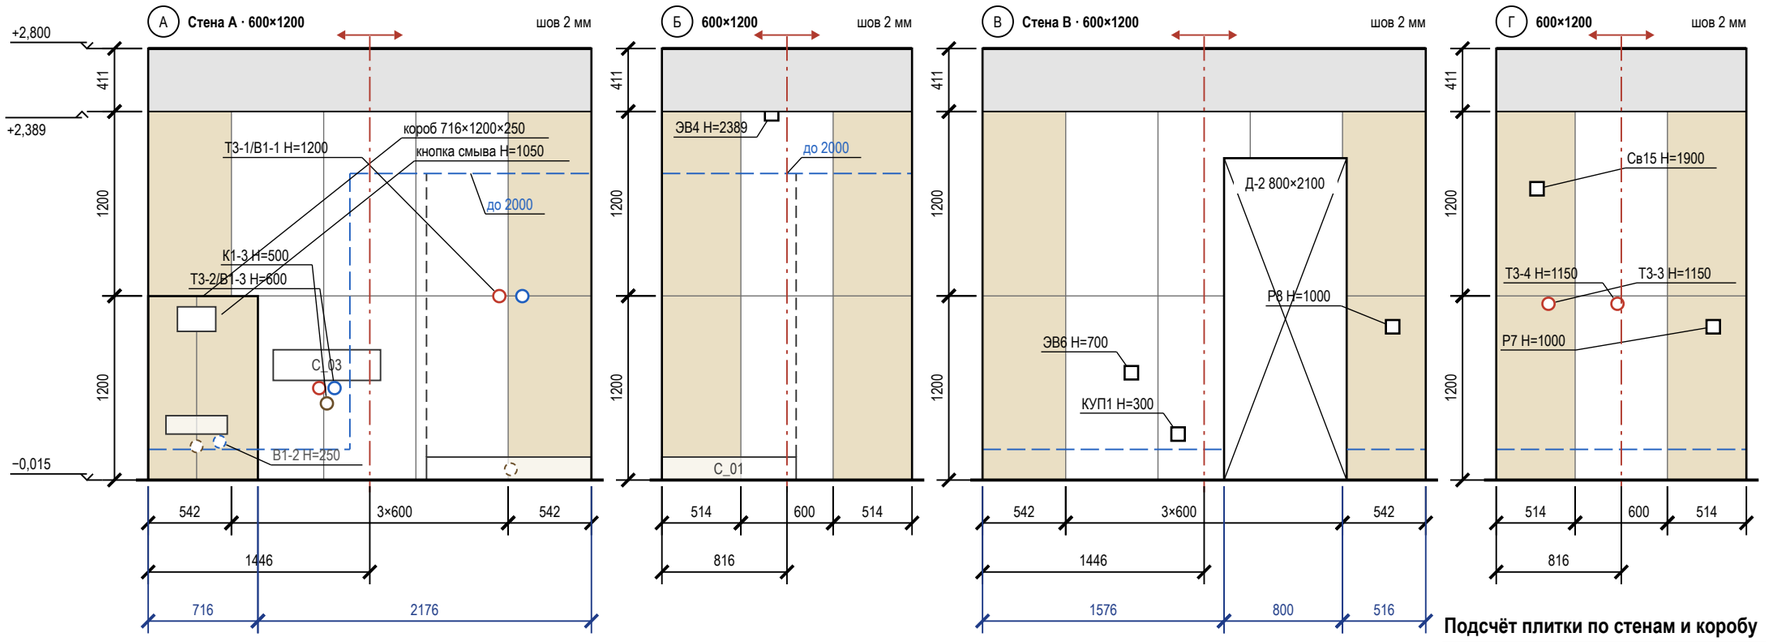

Условные обозначения

- плитка целая; тонкая линия — шов
- плитка с подрезкой (размер — на цепочке)
- ось старта; стрелки — направление укладки
- верх гидроизоляции: 200 от ЧП, в мокрой зоне — «до …»
- проём — не облицовывается
- сантехприбор: габарит, высота по практике
- граница душевой зоны (ограждение)
- короб инсталляции, в нём кнопка смыва 250×160
- вывод В1 (код — в ведомости привязок)
- вывод ТЗ (код — в ведомости привязок)
- вывод К1 (код — в ведомости привязок)
- вывод за прибором / в коробе (не на сетке)
- электроточка: марка и Н — по листам ЭОМ
- отметка уровня, м: ±0,000 — чистый пол жилых помещений
- низ потолка; серая полоса — стена без плитки
- (А) обозначение стены А–Г (как на развёртках)

Примечания

1. Вид изнутри, стены по часовой стрелке А → Г. Высоты — от чистого пола (−0,015), отметки — от ±0,000. Раскладка от чистовых размеров (штукатурка 10 + клей 5 + плитка 9 мм), подрезки чистые; старт — от оси стены, ряды от пола целыми.
2. Верх плитки +2,389, потолок +2,800, зазор 411 мм: потолок ГКЛ опустить до +2,392 (шов 3 мм, герметик) согласовать с монтажником ГКЛ; иначе профиль-окантовка, полосу окрасить в цвет потолка. Подрезной ряд 406 мм не делать.
3. Точки из таблицы сдвигов переносятся до черновой разводки: смеситель — по оси пары В1 + ТЗ; вывод на оси прибора — вместе с прибором, иначе старт раскладки — на ось прибора.
4. За приборами и в коробе (К1-1, В1-2, К1-2) — штриховым кольцом.
5. Гидроизоляция: 200 мм от ЧП по периметру; у душа — до 2000 и 500 мм за поддон (СП 29.13330.2011, п. 7.2 — на высоту замачивания); углы — лентой; акт скрытых работ, пролив.
6. Короб 716×1200×250: лицо 315 / 399 мм от оси кнопки смыва, боковины, полка; углы — запил 45° или профиль; за коробом плитку не кладут.

Подсчёт плитки по стенам и коробу

Поверхность	L × H, мм	S, м²	Целых	Подр.	С запасом	Подрезки: край / верх, мм
стена А	2892 × 2404	6,21	5	4	10	542 / 542; целый ряд
короб (ст. А)	716×1200×250	1,64	0	6	7	лицо 315 / 399; бок. 250
стена Б	1632 × 2404	4,04	2	4	7	514 / 514; целый ряд
стена В	2892 × 2404	5,39	2	7	10	542 / 542; целый ряд
стена Г	1632 × 2404	4,04	2	4	7	514 / 514; целый ряд
Итого		**21,31**	**11**	**25**	**41**	

Сдвиг точек под раскладку

Точка (ВК, ЭОМ)	Стена	Проект: от угла / Н	Под раскладку: от угла / Н	Сдвиг, мм
ТЗ-1/В1-1	А	2366 / 1200	2349 / 1141	−17 на шов; Н −59
ТЗ-2/В1-3, К1-3	А	1166 / 600, 500	1145 / 600, 500	−21 на шов
ЭВ4	Б	716 / 2389	816 / 2403	+100 в центр плитки; Н +14
Р8	В	2676 / 1000	2650 / 1000	−26 в центр плитки
КУП1	В	1276 / 300	1145 / 300	−131 на шов
ЭВ6	В	971 / 700	844 / 700	−127 в центр плитки
ТЗ-3	Г	341 / 1150	214 / 1150	−127 в центр плитки
ТЗ-4	Г	791 / 1150	816 / 1150	+25 в центр плитки
Св15	Г	266 / 1900	214 / 1900	−52 в центр плитки


	Лист	№ док.	Подпись	Дата
Дизайнер	Кырлан А.С.			19.10.26

Проект: Дом 331 м²

Раскладка плитки. Санузел 1 этажа. Развёртки стен

Стадия	Лист	Листов
П	25	155

выпуск 18.10.2026 № ffc1f29499 · стр. 25 из 155

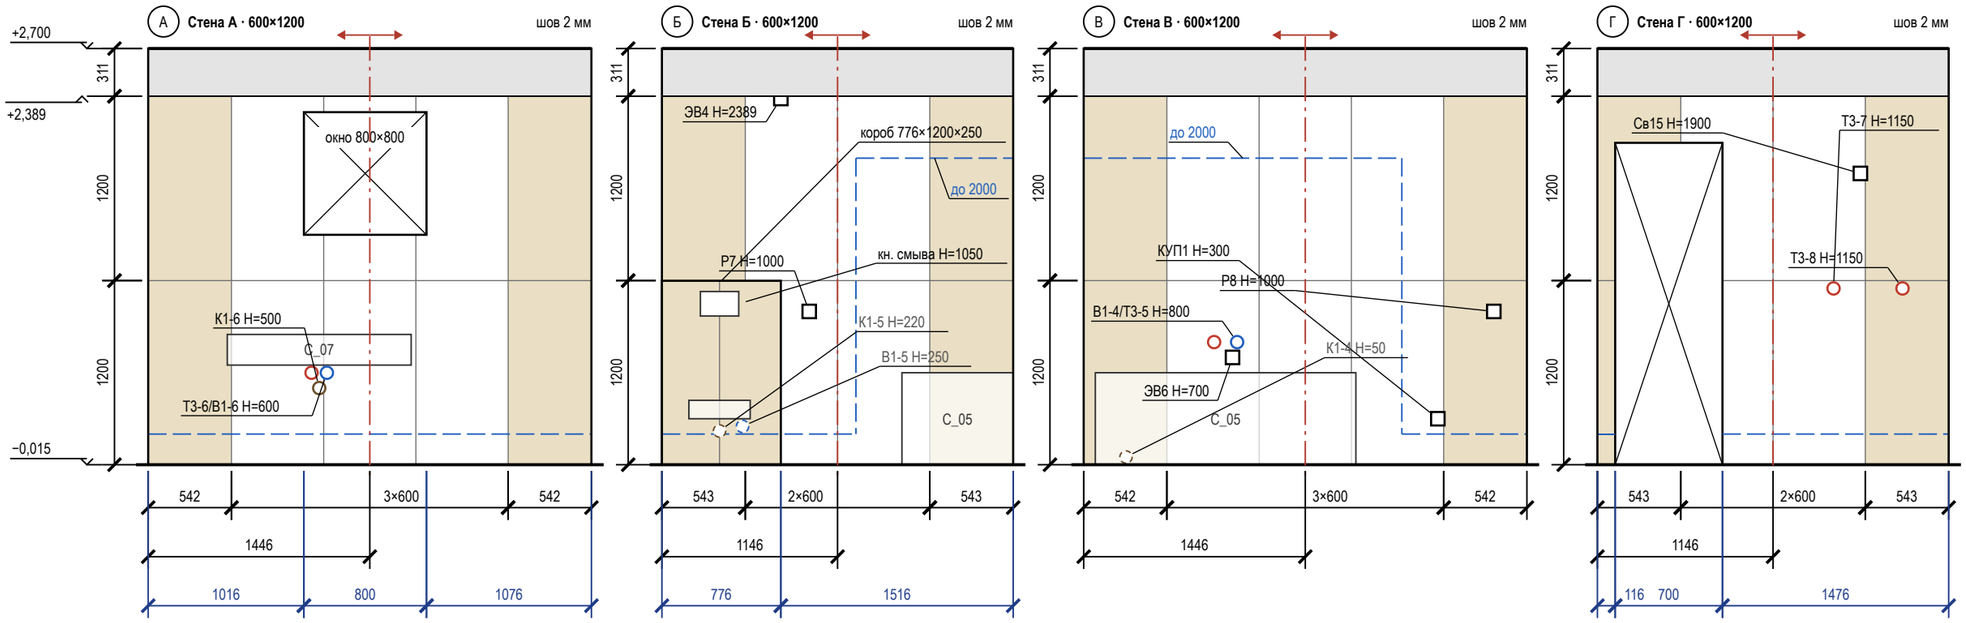

Подсчёт плитки по стенам и коробу

Поверхность	L × H, мм	S, м²	Целых	Подр.	С запасом	Подрезки: край / верх, мм
стена А	2892 × 2404	4,54	3	7	11	542 / 542; целый ряд
стена Б	2292 × 2404	3,97	3	4	8	543 / 543; целый ряд
короб (ст. Б)	776×1200×250	1,73	0	6	7	лицо 375 / 399; бок. 250
стена В	2892 × 2404	7,07	6	4	11	542 / 542; целый ряд
стена Г	2292 × 2404	3,43	2	6	9	543 / 543; целый ряд
Итого		**20,73**	**14**	**27**	**46**	

Сдвиг точек под раскладку

Точка (ВК, ЭОМ)	Стена	Проект: от угла / Н	Под раскладку: от угла / Н	Сдвиг, мм
Т3-6/В1-6, К1-6	А	1116 / 600, 500	1145 / 600, 500	+29 на шов
Р7	Б	961 / 1000	845 / 1000	−116 в центр плитки
ЭВ4	Б	776 / 2389	845 / 2403	+69 в центр плитки; Н +14
В1-4/Т3-5	В	926 / 800	844 / 800	−82 в центр плитки
Р8	В	2676 / 1000	2650 / 1000	−26 в центр плитки
КУП1	В	2311 / 300	2349 / 300	+38 на шов
ЭВ6	В	971 / 700	844 / 700	−127 в центр плитки
Т3-7	Г	1541 / 1150	1447 / 1150	−94 в центр плитки
Т3-8	Г	1991 / 1150	2049 / 1150	+58 в центр плитки
Св15	Г	1716 / 1900	1748 / 1900	+32 на шов

Условные обозначения


- плитка целая; тонкая линия — шов
- плитка с подрезкой (размер — на цепочке)
- ось старта; стрелки — направление укладки
- верх гидроизоляции: 200 от ЧП, в мокрой зоне — «до …»
- проём — не облицовывается
- сантехприбор: габарит, высота по практике
- короб инсталляции, в нём кнопка смыва 250×160
- вывод В1 (код — в ведомости привязок)
- вывод Т3 (код — в ведомости привязок)
- вывод К1 (код — в ведомости привязок)
- вывод за прибором / в коробе (не на сетке)
- электроточка: марка и Н — по листам ЭОМ
- отметка уровня, м: ±0,000 — чистый пол жилых помещений
- низ потолка; серая полоса — стена без плитки
- обозначение стены А–Г (как на развёртках)

Примечания

1. Вид изнутри, стены по часовой стрелке А → Г. Высоты — от чистого пола (−0,015), отметки — от ±0,000. Раскладка от чистовых размеров (штукатурка 10 + клей 5 + плитка 9 мм), подрезки чистые; старт — от оси стены, ряды от пола целыми.
2. Верх плитки +2,389, потолок +2,700, зазор 311 мм: потолок ГКЛ опустить до +2,392 (шов 3 мм, герметик) — согласовать с монтажником ГКЛ; иначе профиль-окантовка, полосу окрасить в цвет потолка. Подрезной ряд 306 мм не делать.
3. Точки из таблицы сдвигов переносятся до черновой разводки: смеситель — по оси пары В1 + Т3; вывод на оси прибора вместе с прибором, иначе старт раскладки — на ось прибора.
4. За приборами и в коробе (В1-5, К1-5, К1-4) — штриховым кольцом.
5. Гидроизоляция: 200 мм от ЧП по периметру; над ванной — до 2000 и 300 мм за борт (СП 29.13330.2011, п. 7.2 — на высоту замачивания); углы — лентой; акт скрытых работ, пролив.
6. Короб 776×1200×250: лицо 375 / 399 мм от оси кнопки смыва, боковины, полка; углы — запил 45° или профиль; за коробом плитку не кладут.

					Проект: Дом 331 м²
	Лист	№ док.	Подпись	Дата	Раскладка плитки. Санузел мастер. Развёртки стен
Дизайнер	Кырлан А.С.			19.10.26	Стадия: П; Лист: 26; Листов: 155

выпуск 18.10.2026 № ffc1f29499 · стр. 26 из 155

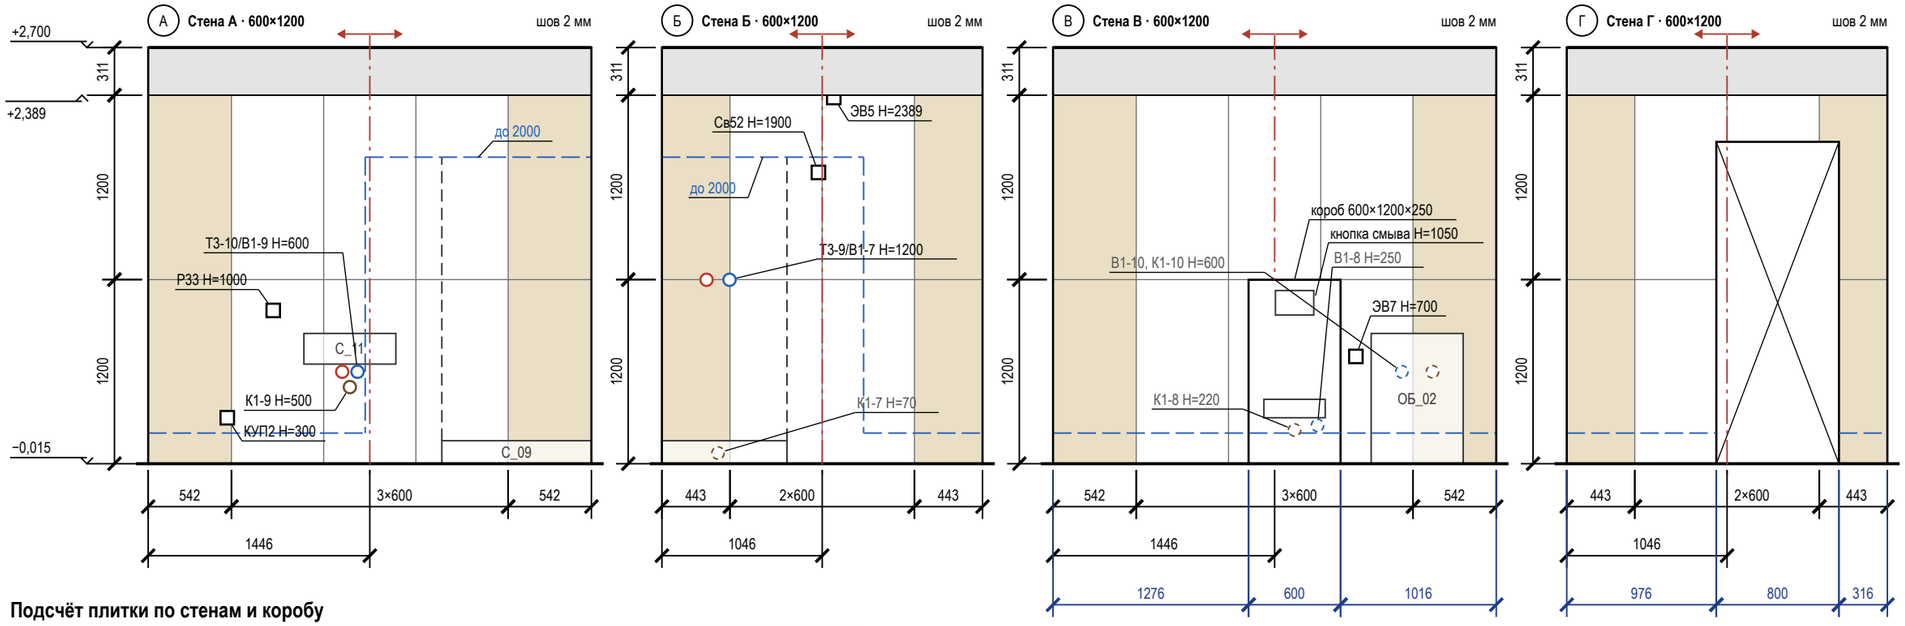

Подсчёт плитки по стенам и коробу

Поверхность	L × H, мм	S, м²	Целых	Подр.	С запасом	Подрезки: край / верх, мм
стена А	2892 × 2404	7,07	6	4	11	542 / 542; целый ряд
стена Б	2092 × 2404	4,42	4	4	9	443 / 443; целый ряд
стена В	2892 × 2404	2,81	4	6	11	542 / 542; целый ряд
короб (ст. В)	600×1200×250	1,47	1	3	5	лицо 600; бок. 250
стена Г	2092 × 2404	2,74	0	7	8	443 / 443; целый ряд
Итого		**18,51**	**15**	**24**	**44**	

Сдвиг точек под раскладку

Точка (ВК, ЭОМ)	Стена	Проект: от угла / Н	Под раскладку: от угла / Н	Сдвиг, мм
Т3-10/В1-9, К1-9	А	1316 / 600, 500	1446 / 600, 500	+130 в центр плитки
Р33	А	816 / 1000	844 / 1000	+28 в центр плитки
КУП2	А	516 / 300	543 / 300	+27 на шов
Т3-9/В1-7	Б	366 / 1200	444 / 1141	+78 на шов; Н −59
Св52	Б	1021 / 1900	1046 / 1900	+25 на шов
ЭВ5	Б	1121 / 2389	1046 / 2343	−75 на шов; Н −46
ЭВ7	В	1976 / 700	2048 / 700	+72 в центр плитки

Условные обозначения

- плитка целая; тонкая линия — шов
- плитка с подрезкой (размер — на цепочке)
- ось старта; стрелки — направление укладки
- верх гидроизоляции: 200 от ЧП, в мокрой зоне — «до …»
- проём — не облицовывается
- сантехприбор: габарит, высота по практике
- граница душевой зоны (ограждение)
- короб инсталляции, в нём кнопка смыва 250×160
- вывод В1 (код — в ведомости привязок)
- вывод Т3 (код — в ведомости привязок)
- вывод К1 (код — в ведомости привязок)
- вывод за прибором / в коробе (не на сетке)
- электроточка: марка и Н — по листам ЭОМ
- отметка уровня, м: ±0,000 — чистый пол жилых помещений
- низ потолка; серая полоса — стена без плитки
- (А) обозначение стены А–Г (как на развёртках)

Примечания

1. Вид изнутри, стены по часовой стрелке А → Г. Высоты — от чистого пола (−0,015), отметки — от ±0,000. Раскладка от чистовых размеров (штукатурка 10 + клей 5 + плитка 9 мм), подрезки чистые; старт — от оси стены, ряды от пола целыми.
2. Верх плитки +2,389, потолок +2,700, зазор 311 мм: потолок ГКЛ опустить до +2,392 (шов 3 мм, герметик) согласовать с монтажником ГКЛ; иначе профиль-окантовка, полосу окрасить в цвет потолка. Подрезной ряд 306 мм не делать.
3. Точки из таблицы сдвигов переносятся до черновой разводки: смеситель — по оси пары В1 + Т3; вывод на оси прибора — вместе с прибором, иначе старт раскладки — на ось прибора.
4. За приборами и в коробе (К1-7, В1-8, К1-8, В1-10, К1-10) — штриховым кольцом.
5. Гидроизоляция: 200 мм от ЧП по периметру; у душа — до 2000 и 500 мм за поддон (СП 29.13330.2011, п. 7.2 — на высоту замачивания); углы — лентой; акт скрытых работ, пролив.
6. Короб 600×1200×250: лицо 600 мм от оси кнопки смыва, боковины, полка; углы — запил 45° или профиль; за коробом плитку не кладут.

	Лист	№ док.	Подпись	Дата
Дизайнер	Кырлан А.С.			19.10.26

Проект: Дом 331 м²


Раскладка плитки. Санузел 2. Развёртки стен

Стадия	Лист	Листов
П	27	155

выпуск 18.10.2026 № ffc1f29499 · стр. 27 из 155

Примечания

1. Размеры проёмов и привязки — в миллиметрах от чистых граней стен до отделки; привязка — от угла того помещения, со стороны которого стоит размер. Размер в ведомости — ширина × высота проёма от чистого пола 0,000.
2. Марки в кружках — типы заполнения проёмов (ГОСТ 21.501-2018, п. 5.3.2); одна марка — один типоразмер; количество сверено с планом.
3. Открывание: Л — петли слева, П — справа, если смотреть со стороны, куда открывается полотно (на себя).
4. Дверные блоки обычного монтажа (Д-4…Д-6, Д-14) заказывать после чистовой стяжки и штукатурки, проёмы перемерить; монтажный зазор коробки 10–15 мм на сторону, откос от угла помещения до коробки не менее 50 мм.
5. Скрытые двери (Д-1, Д-2): проём замерить в чистоте; блок заказать до штукатурки (≈ 30 дн.), короб ставить до штукатурки; полотно навесить после чистовой отделки, красить в цвет стен. Порядок практика монтажа, изготовитель подтверждает.
6. Д-1, Д-2 — существующие проёмы, до техзаключения не расширять.

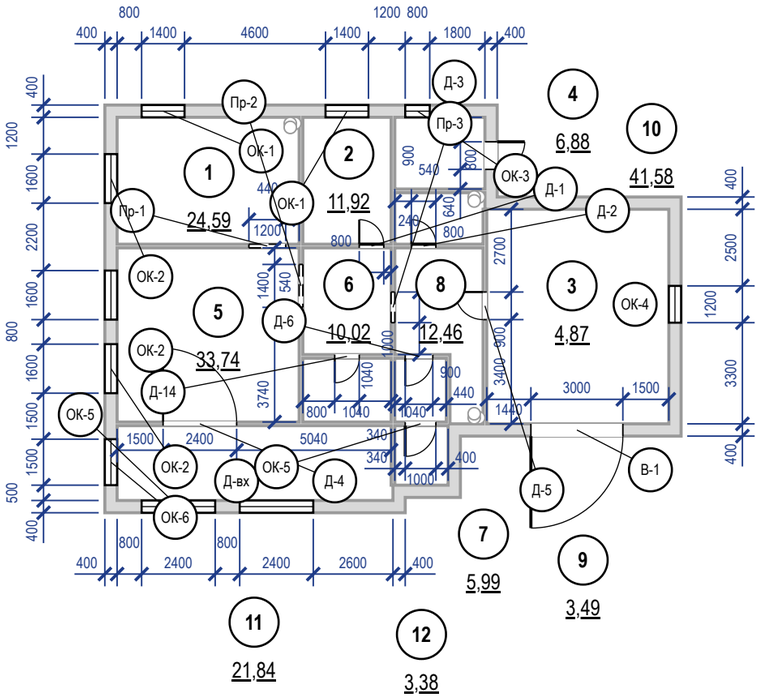

Ведомость заполнения проёмов


Марка	Наименование, обозначение	Проём ш×в, мм	Кол.	Откр.	Отделка полотна	Фурнитура	Прим.
Д-вх	Блок дверной входной, ГОСТ 31173-2016	1000×2100	1	Л	в комплекте блока	в комплекте блока (замки, глазок)	наружу
В-1	Блок дверной входной, ГОСТ 31173-2016	3000×2300	1	Л	в комплекте блока	в комплекте блока (замки, глазок)	наружу
Д-1	Дверь скрытого монтажа, ТУ изготовителя	800×2100	1	П	окраска No. 226 с двух сторон	скрытые петли 3D, магнитный замок	
Д-2	Дверь скрытого монтажа, ТУ изготовителя	800×2100	1	П	в тон облицовки — пом. 3, No. 226 — пом. 8	скрытые петли 3D, магнитный замок, фиксатор WC	порог 15
Д-3	Блок дверной входной, ГОСТ 31173-2016	900×2100	1	П	в комплекте блока	в комплекте блока (замки, глазок)	наружу
Д-4	Блок дверной внутренний, остекл., ГОСТ 475-2016	2400×2100	1	П		петли, ручка с защёлкой	
Д-5	Блок дверной внутренний, ГОСТ 475-2016	900×2100	1	Л		петли, ручка с защёлкой	
Д-6	Блок дверной внутренний, ГОСТ 475-2016	900×2100	1	Л		петли, ручка с защёлкой	
Д-14	Блок дверной внутренний, ГОСТ 475-2016	800×2100	1	Л		петли, ручка с защёлкой	
Пр-1	Портал без заполнения	1200×2100	1				б/п
Пр-2	Портал без заполнения	1400×2100	1				б/п
Пр-3	Портал без заполнения	1000×2100	1				б/п
ОК-1	Блок оконный, ГОСТ 23166-2021	1400×1500	2				низ 900
ОК-2	Блок оконный, ГОСТ 23166-2021	1600×1500	3				низ 900
ОК-3	Блок оконный, ГОСТ 23166-2021	800×900	1				низ 1200
ОК-4	Блок оконный, ГОСТ 23166-2021	1200×900	1				низ 1200
ОК-5	Блок оконный, ГОСТ 23166-2021	2400×1600	2				низ 900
ОК-6	Блок оконный, ГОСТ 23166-2021	1500×1600	1				низ 900

					Проект: Дом 331 м²		
	Лист	№ док.	Подпись	Дата	План размещения дверей · 1-й этаж	Стадия	Лист	Листов
Дизайнер	Кырлан А.С.			19.10.26		П	28	155

выпуск 18.10.2026 № ffc1f29499 · стр. 28 из 155

Примечания

1. Размеры проёмов и привязки — в миллиметрах от чистых граней стен до отделки; привязка — от угла того помещения, со стороны которого стоит размер. Размер в ведомости — ширина × высота проёма от чистого пола 0,000. Откос от угла помещения до проёма с коробкой — не менее 50 мм.
2. Марки в кружках — типы заполнения проёмов (ГОСТ 21.501-2018, п. 5.3.2); одна марка — один типоразмер; количество сверено с планом.
3. Открывание: Л — петли слева, П — справа, если смотреть со стороны, куда открывается полотно (на себя).
4. Скрытые двери (Д-7…Д-13): проём замерить в чистоте; блок заказать до штукатурки (≈ 30 дн.), короб ставить до штукатурки; полотно навесить после чистовой отделки, красить в цвет стен. Порядок практика монтажа, изготовитель подтверждает.
5. Д-7…Д-13 — существующие проёмы, до техзаключения не расширять.

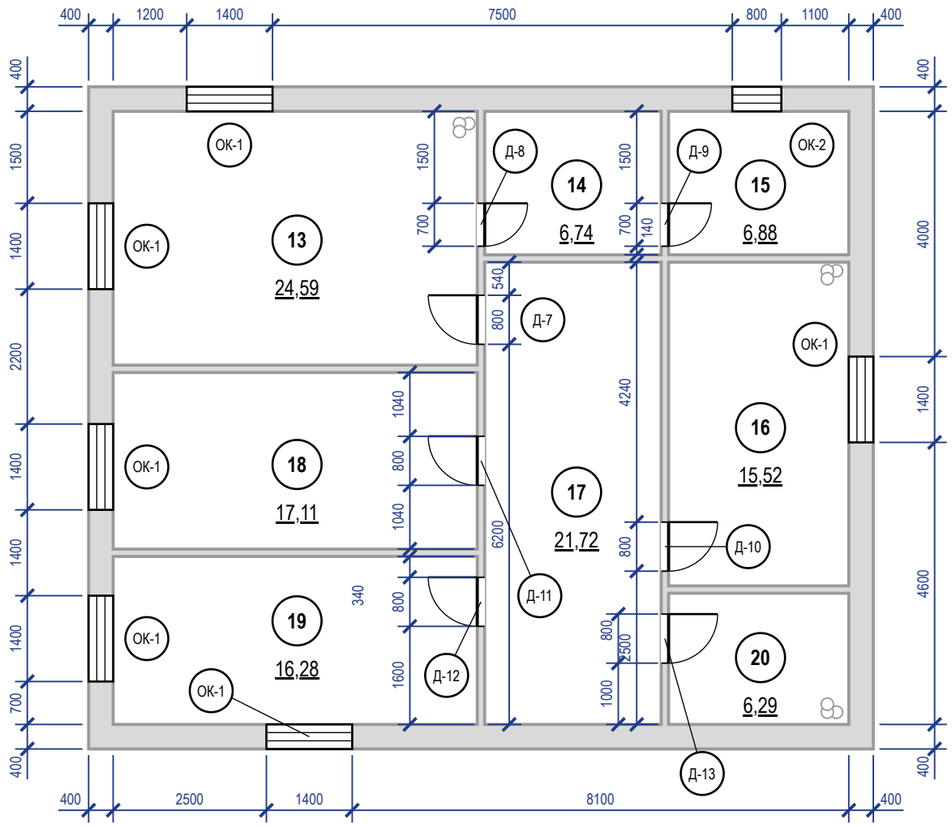


Ведомость заполнения проёмов

Марка	Наименование, обозначение	Проём ш×в, мм	Кол.	Откр.	Отделка полотна	Фурнитура	Прим.
Д-7	Дверь скрытого монтажа, ТУ изготовителя	800×2100	1	Л	окраска No. 226 с двух сторон	скрытые петли 3D, магнитный замок	
Д-8	Дверь скрытого монтажа, ТУ изготовителя	700×2100	1	П	No. 105 — пом. 14, No. 226 — пом. 13	скрытые петли 3D, магнитный замок	
Д-9	Дверь скрытого монтажа, ТУ изготовителя	700×2100	1	П	в тон облицовки — пом. 15, No. 105 — пом. 14	скрытые петли 3D, магнитный замок, фиксатор WC	порог 15
Д-10	Дверь скрытого монтажа, ТУ изготовителя	800×2100	1	П	окраска No. 226 с двух сторон	скрытые петли 3D, магнитный замок	
Д-11	Дверь скрытого монтажа, ТУ изготовителя	800×2100	1	Л	окраска No. 226 с двух сторон	скрытые петли 3D, магнитный замок	
Д-12	Дверь скрытого монтажа, ТУ изготовителя	800×2100	1	Л	окраска No. 226 с двух сторон	скрытые петли 3D, магнитный замок	
Д-13	Дверь скрытого монтажа, ТУ изготовителя	800×2100	1	П	в тон облицовки — пом. 20, No. 226 — пом. 17	скрытые петли 3D, магнитный замок, фиксатор WC	порог 15
ОК-1	Блок оконный, ГОСТ 23166-2021	1400×1500	6				низ 900
ОК-2	Блок оконный, ГОСТ 23166-2021	800×800	1				низ 1500


					Проект: Дом 331 м²		
	Лист	№ док.	Подпись	Дата	План размещения дверей · Мансарда	Стадия	Лист	Листов
Дизайнер	Кырлан А.С.			19.10.26		П	29	155

выпуск 18.10.2026 № ffc1f29499 · стр. 29 из 155

План марша Л-1 (М 1:50) · 6. Холл с лестницей

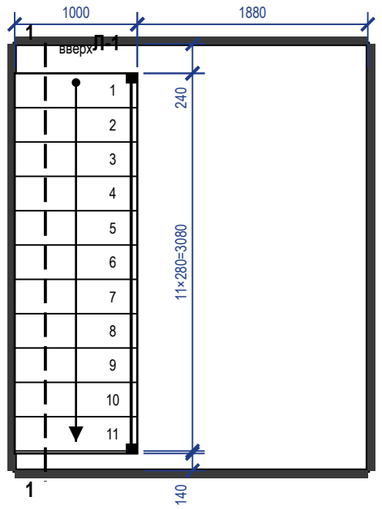


Разрез 1-1 (М 1:50)

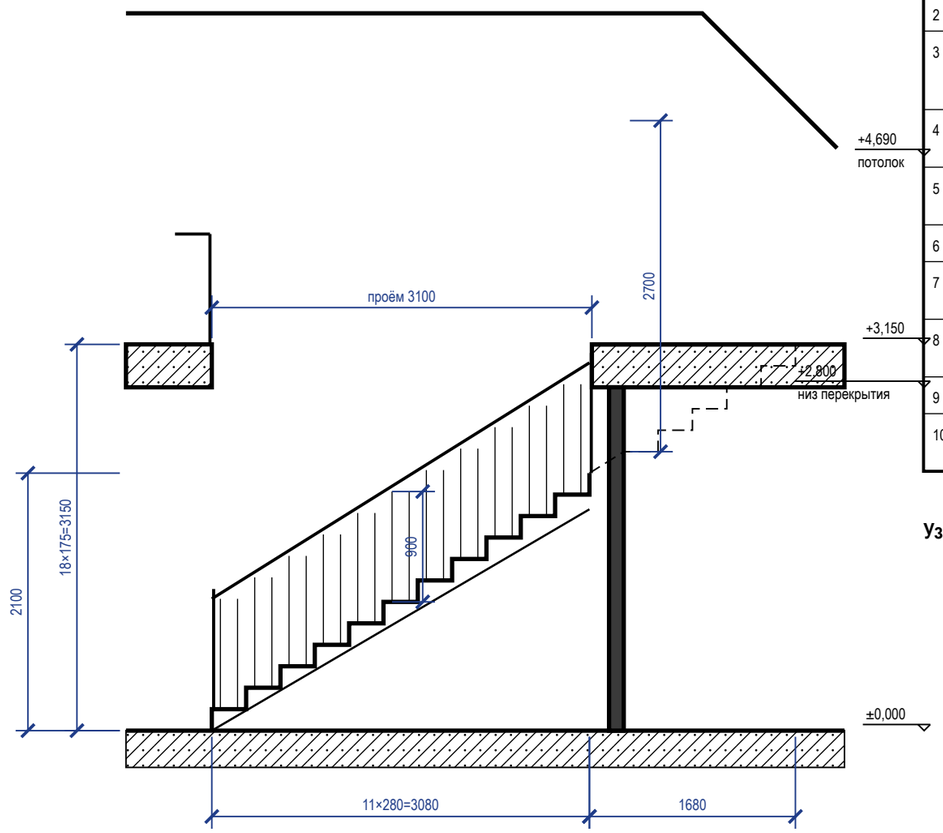

Спецификация элементов лестницы Л-1

Поз.	Наименование	Кол.	Материал, сечение	Примечание
1	Ступень (проступь)	17	дуб, массив 40 мм, масло	1000×280, толщина по изделию
2	Подступенок	18	дуб 18 мм	высота 175
3	Косоур	2	косоуры стальные 80×40×4, порошковая окраска	несущие марша
4	Столб ограждения марша	2	сталь 20×20, порошковая окраска	по концам марша, стороны Б
5	Балясина	46	сталь 20×20, порошковая окраска	шаг 120, просвет 100
6	Поручень марша	1	дуб 40×60	L ≈ 5,61 м, h 900
7	Столб ограждения проёма	3	сталь 20×20, порошковая окраска	углы проёма, стороны А, Б
8	Балясина ограждения проёма	34	сталь 20×20, порошковая окраска	шаг 120
9	Поручень ограждения проёма	1	дуб 40×60	L ≈ 4,10 м, h 900
10	Крепёж ограждения	1	комплект по изделию	нагрузка на поручень 0,5 кН/м

Узел 1. Крепление стойки ограждения (М 1:5)

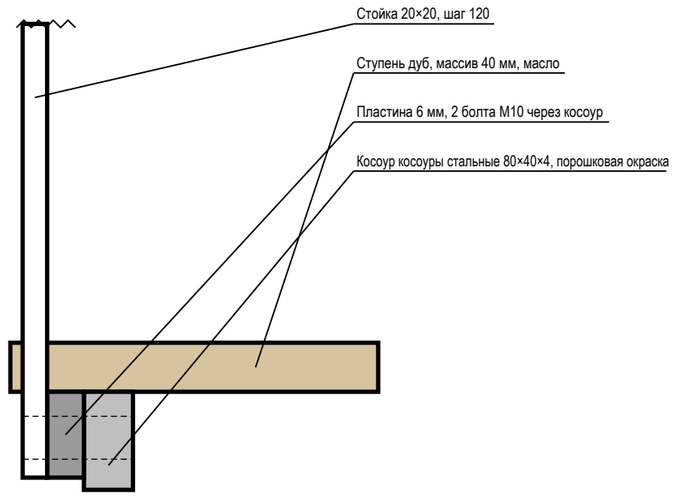

Зазор заполнения до ступени 100 (ГОСТ 25772, прил. А); узел типовой, уточнить по изделию


Примечания

1. Лестница Л-1: 18 подъёмов × 175 мм = 3150 мм (отм. ±0,000 … +3,150), проступь 280 мм, ширина марша 1000 мм; уклон 32,0°, шаг 2h + b = 630 мм (удобно 600–640 — практика).
2. В габарит марша 3100 мм входят 11 проступей (до отм. +2,100); до пола этажа выше нужно 17 проступей — 4760 мм (показаны штрихом): одномаршевая лестница в этом помещении не встаёт, решение по реестру.
3. Ограждение марша со стороны Б: балясины, просвет между элементами 100 мм (не больше 150 — ГОСТ 25772-2025, табл. 3, тип МВ); высота 900 мм, поручень с одной стороны на 900 мм по линии носков (не менее 900 — СП 55.13330.2016, п. 8.3; СП 59.13330.2020, п. 6.2.11).
4. Проём в перекрытии 1000×3100 мм на этаже 2 ограждён со сторон А, Б высотой 900 мм, непрерывно, с поручнем (СП 55.13330.2016, п. 8.3); нагрузка на поручень 0,5 кН/м (СП 20.13330.2016, п. 8.2.6).
5. Просвет над линией носков — не менее 2700 мм (ступень 13, под потолком мансарды); рекомендуется не менее 2000, путь эвакуации — 2200 (СП 55.13330.2016, п. 7.4).
6. Все подступенки одной высоты (СП 55.13330.2016, п. 8.2). Размеры по месту уточнить после обмера: разность отметок чистых полов замерить до заказа изделия.
7. Узел 1 — типовое решение крепления стойки к косоуру; крепёж, сечения и материал — по проекту изделия изготовителя лестницы.

					Проект: Дом 331 м²
	Лист	№ док.	Подпись	Дата	
Дизайнер	Кырлан А.С.			19.10.26	Лестница Л-1

Стадия	Лист	Листов
П	30	155

выпуск 18.10.2026 № ffc1f29499 · стр. 30 из 155

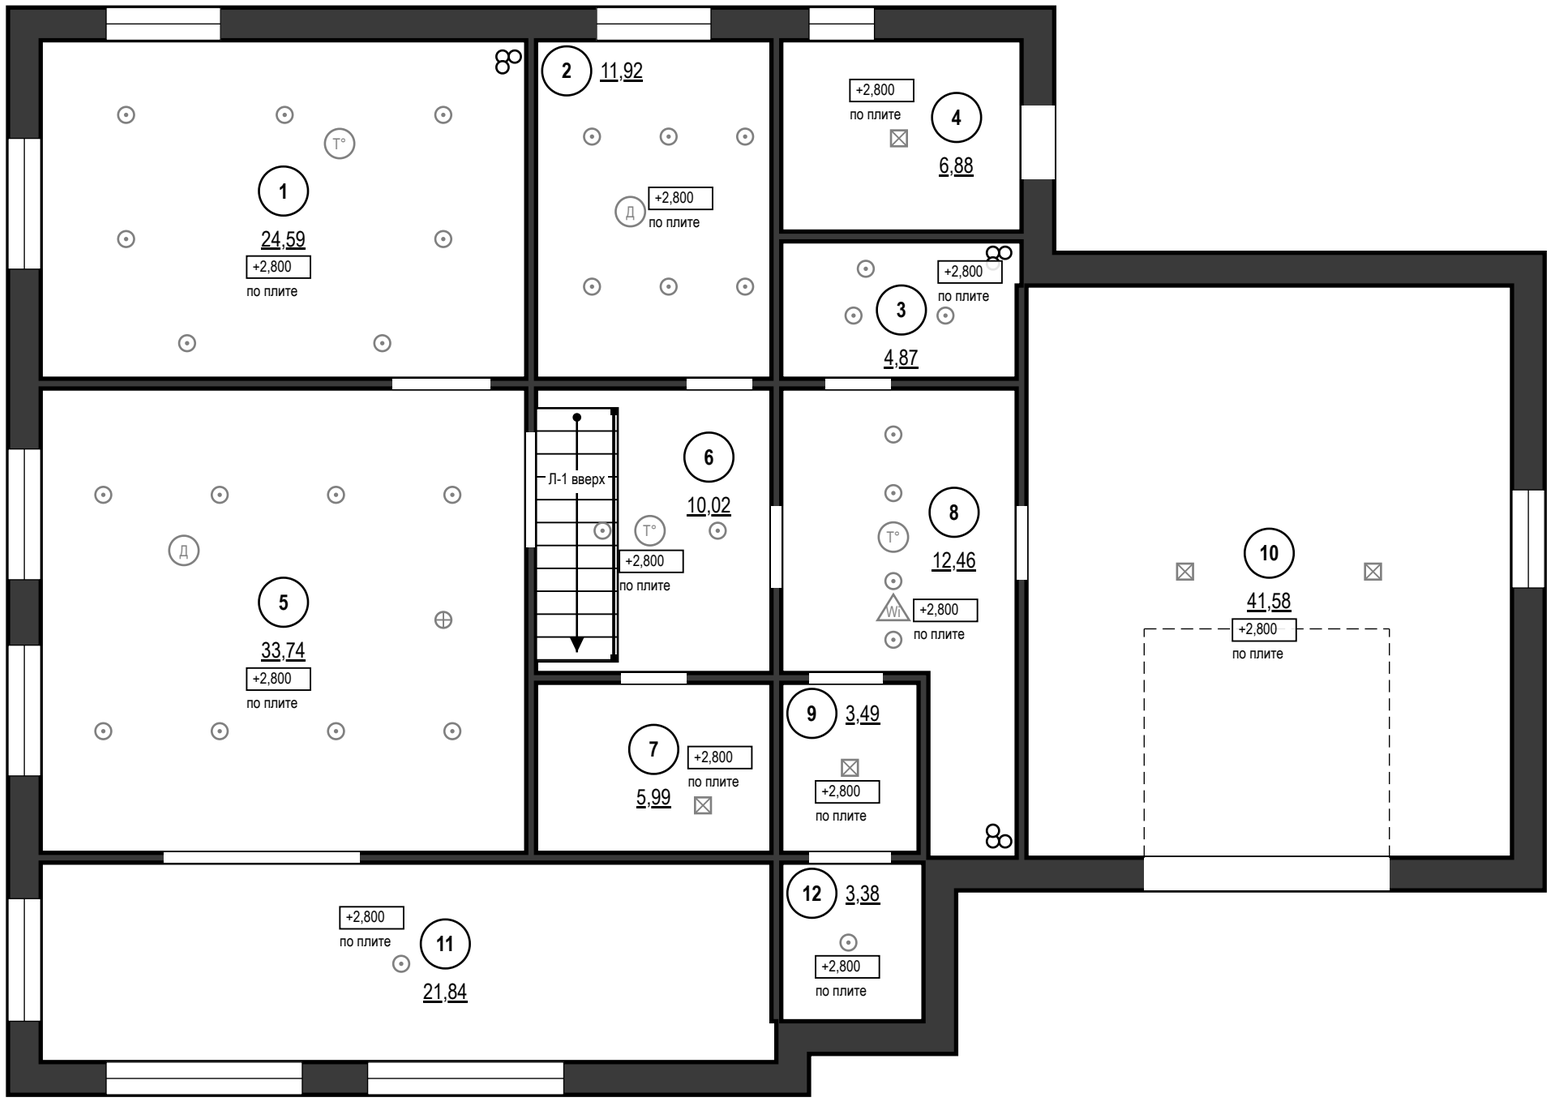

Ведомость потолков

Пом.	Марка	Конструкция	Низ	S, м²	Q
1		по плите, окраска	+2,800	24,59	
2		по плите, окраска	+2,800	11,92	
3		по плите, окраска	+2,800	4,87	
4		по плите, окраска	+2,800	6,88	
5		по плите, окраска	+2,800	33,74	
6		по плите, окраска	+2,800	10,02	
7		по плите, окраска	+2,800	5,99	
8		по плите, окраска	+2,800	12,46	
9		по плите, окраска	+2,800	3,49	
10		по плите, окраска	+2,800	41,58	
11		по плите, окраска	+2,800	21,84	
12		по плите, окраска	+2,800	3,38	
		Итого		**180,76**	

Ведомость вырезов и закладных в потолке

Марка	Устройство	Кол.	Пом.
	Светильник встраиваемый (марки — план освещения)	32	1, 2, 3, 5, 6, 8, 11, 12
	Светильник накладной (марки — план освещения)	5	4, 7, 9, 10
	Светильник подвесной (марки — план освещения)	1	5
ИП2, ИП1	Извещатель дымовой	2	2, 5
ИП4, ИП6, ИП3	Извещатель тепловой	3	1, 6, 8
AP1	Точка доступа Wi-Fi, PoE	1	8

Примечания

1. За отметку ±0,000 принят уровень чистого пола сухих помещений (готовое покрытие), а не существующего пола; пол пом. 3, 11, 12 — −0,015, −0,030; существующий пол снимается до плиты, его отметка не замерена. Отметки в прямоугольниках — низ потолка; низ плиты перекрытия +2,800. Марка потолка — одна конструкция и отметка на весь альбом.
2. Светильники и потолочные устройства — подложка с планов освещения, слаботочных систем и вентиляции (положение — по ним); вырезы и закладные — по ведомости на листе, до обшивки; отверстия не совмещать с профилями.
3. Пом. 1, 2, 3, 4, 5, 6, 7, 8, 9, 10, 11, 12 — потолок по плите без подвесной системы; отделка — по ведомости отделки.


	Лист	№ док.	Подпись	Дата
Дизайнер	Кырлан А.С.			19.10.26

Проект: Дом 331 м²

План потолков · 1-й этаж

Стадия	Лист	Листов
П	31	155

выпуск 18.10.2026 № ffc1f29499 · стр. 31 из 155

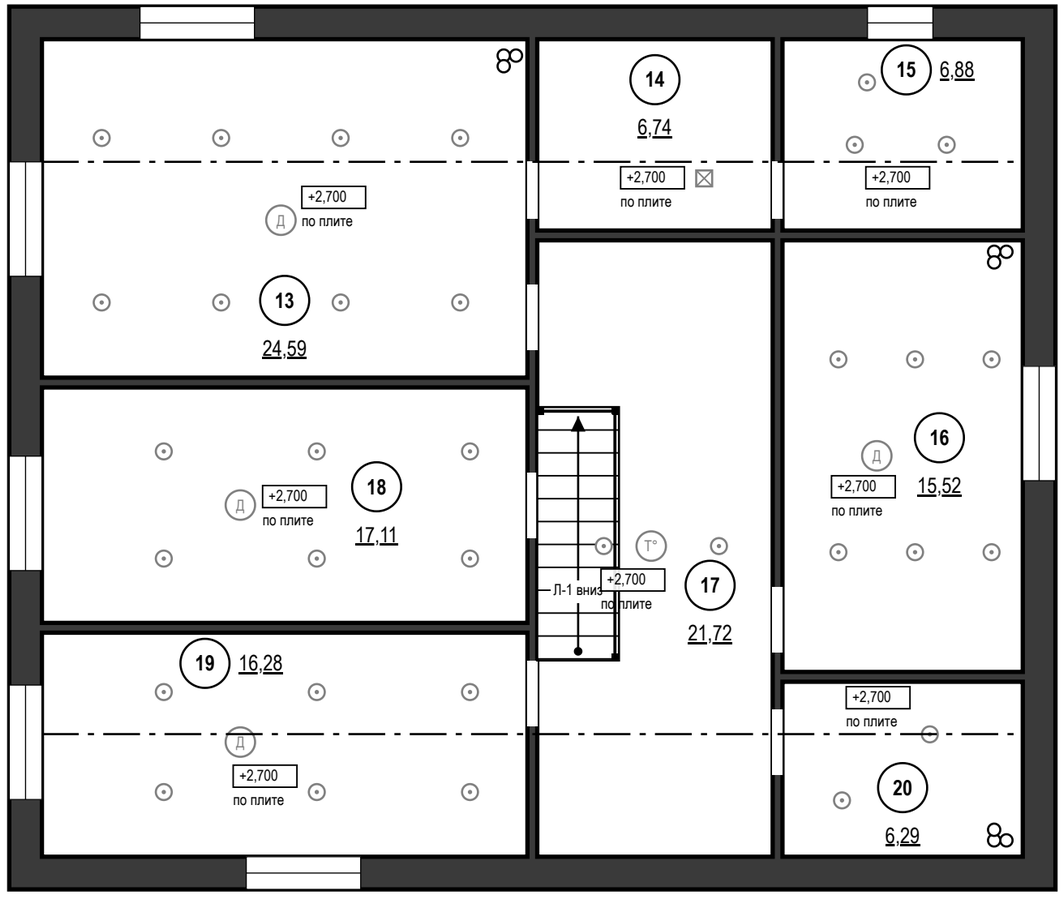

Ведомость потолков

Пом.	Марка	Конструкция	Низ	S, м²	Q
13		по плите, окраска	+2,700	24,59	
14		по плите, окраска	+2,700	6,74	
15		по плите, окраска	+2,700	6,88	
16		по плите, окраска	+2,700	15,52	
17		по плите, окраска	+2,700	21,72	
18		по плите, окраска	+2,700	17,11	
19		по плите, окраска	+2,700	16,28	
20		по плите, окраска	+2,700	6,29	
		Итого		**115,13**	


Ведомость вырезов и закладных в потолке

Марка	Устройство	Кол.	Пом.
	Светильник встраиваемый (марки — план освещения)	33	13, 15, 16, 17, 18, 19, 20
	Светильник накладной (марки — план освещения)	1	14
ИП1, ИП2, ИП2, ИП2	Извещатель дымовой	4	13, 16, 18, 19
ИП6	Извещатель тепловой	1	17

Примечания

1. За отметку ±0,000 принят уровень чистого пола сухих помещений (готовое покрытие), а не существующего пола; пол пом. 15, 20 — −0,015; верх плиты перекрытия −0,064 — расчётный по пирогу пола, не замерен; существующий пол снимается до плиты, его отметка не замерена. Отметки в прямоугольниках — низ потолка; низ плиты перекрытия +2,700. Марка потолка — одна конструкция и отметка на весь альбом.
2. Мансарда: потолок по скатам кровли — от +1,200 у наружных стен вдоль конька до +2,700 у линий перелома (штрихпунктир), между ними горизонтальная часть +2,700; над слуховыми окнами скат поднят до горизонтальной части. Обшивка скатов — по стропилам с пароизоляцией по проекту КР.
3. Светильники и потолочные устройства — подложка с планов освещения, слаботочных систем и вентиляции (положение — по ним); вырезы и закладные — по ведомости на листе, до обшивки; отверстия не совмещать с профилями.
4. Пом. 13, 14, 15, 16, 17, 18, 19, 20 — потолок по плите без подвесной системы; отделка — по ведомости отделки.

					Проект: Дом 331 м²
	Лист	№ док.	Подпись	Дата	План потолков · Мансарда
Дизайнер	Кырлан А.С.			19.10.26	Стадия: П; Лист: 32; Листов: 155

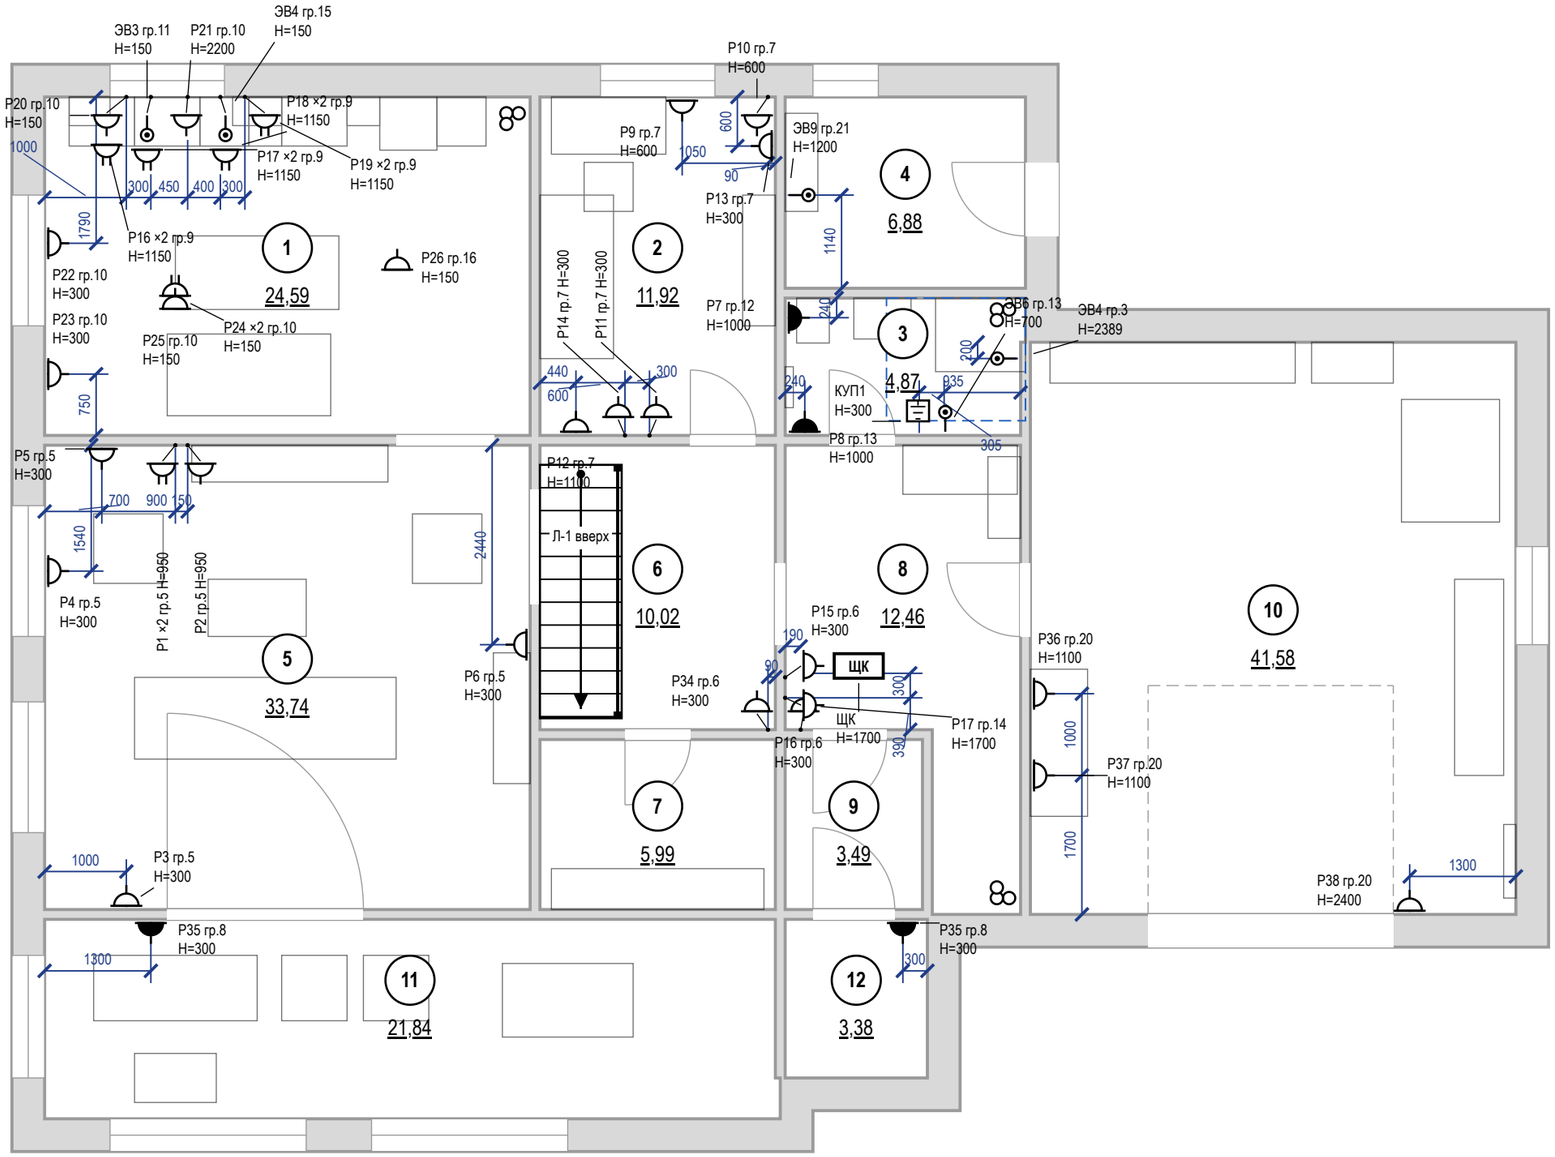

Условные обозначения

- розетка с заземляющим контактом; у знака марка, ×N — постов в рамке, гр. — группа щита, H — высота оси, мм
- то же, рамка на 2 поста (число черточек — число постов)
- розетка влагозащищённая IP44
- вывод кабеля для подключения прибора (без розетки), марка ЭВ
- КУП — коробка уравнивания потенциалов (ДСУП), проводник к шине PE щита
- ЩК — щит квартирный
- знак разведён для читаемости: точка на стене у выноски, привязка — до неё
- граница зоны 2 ванной (600 мм от ванны/поддона)
- мебель и сантехприборы — подложка
- стояк: К1 — канализация, В1 — ХВС, Т3 — ГВС
- 1 — номер помещения, площадь м²


Примечания

1. За отметку 0,000 принят уровень чистого пола. Высоты H — от чистого пола до оси изделия; привязки — от чистовой грани стены до оси механизма (у рамки на несколько постов — до оси рамки).
2. Высота установки, не указанная на плане: розетки — 300 мм от чистого пола; выводы кабеля — по паспорту прибора.
3. Розетки в санузле — только вне зон 0–2 (ПУЭ 7.1.48, ГОСТ Р 50571.7.701-2024), IP44, через УЗО 30 мА.
4. Розеточные и мокрые линии — через УЗО или дифавтомат с током утечки не более 30 мА (ПУЭ 7.1.79); в санузле выполнить ДСУП (ПУЭ 7.1.87–7.1.88).
5. Кабель — медный, исполнение нг(A)-LS (ГОСТ 31565-2012); скрытая прокладка только горизонтально и вертикально, фактические трассы зафиксировать исполнительной схемой до закрытия отделкой.
6. Расчёт нагрузок, токов КЗ, селективности и сечений — по проекту ЭОМ организации с допуском СРО; лист задаёт состав, расположение и группы.
7. Выводы кухонной техники — после утверждения проекта кухни (ориентировочно); привязки выводов даны от осей модулей гарнитура и пересматриваются вместе с проектом кухни.
8. Электрический тёплый пол проектом не предусмотрен; при решении заказчика устроить — отдельный лист «План тёплых полов»: контуры с отступом 100 мм от стен и мебели без ножек, датчик в гофре, терморегулятор, своя группа щита через УЗО 30 мА.
9. Ведомости электроточек, изделий, светильников и расшифровка клавиш — лист «Ведомость электроточек и изделий».

					Проект: Дом 331 м²
	Лист	№ док.	Подпись	Дата	
Дизайнер	Кырлан А.С.			19.10.26	План розеток и электровыводов · 1-й этаж

Стадия	Лист	Листов
П	33	155

выпуск 18.10.2026 № ffc1f29499 · стр. 33 из 155

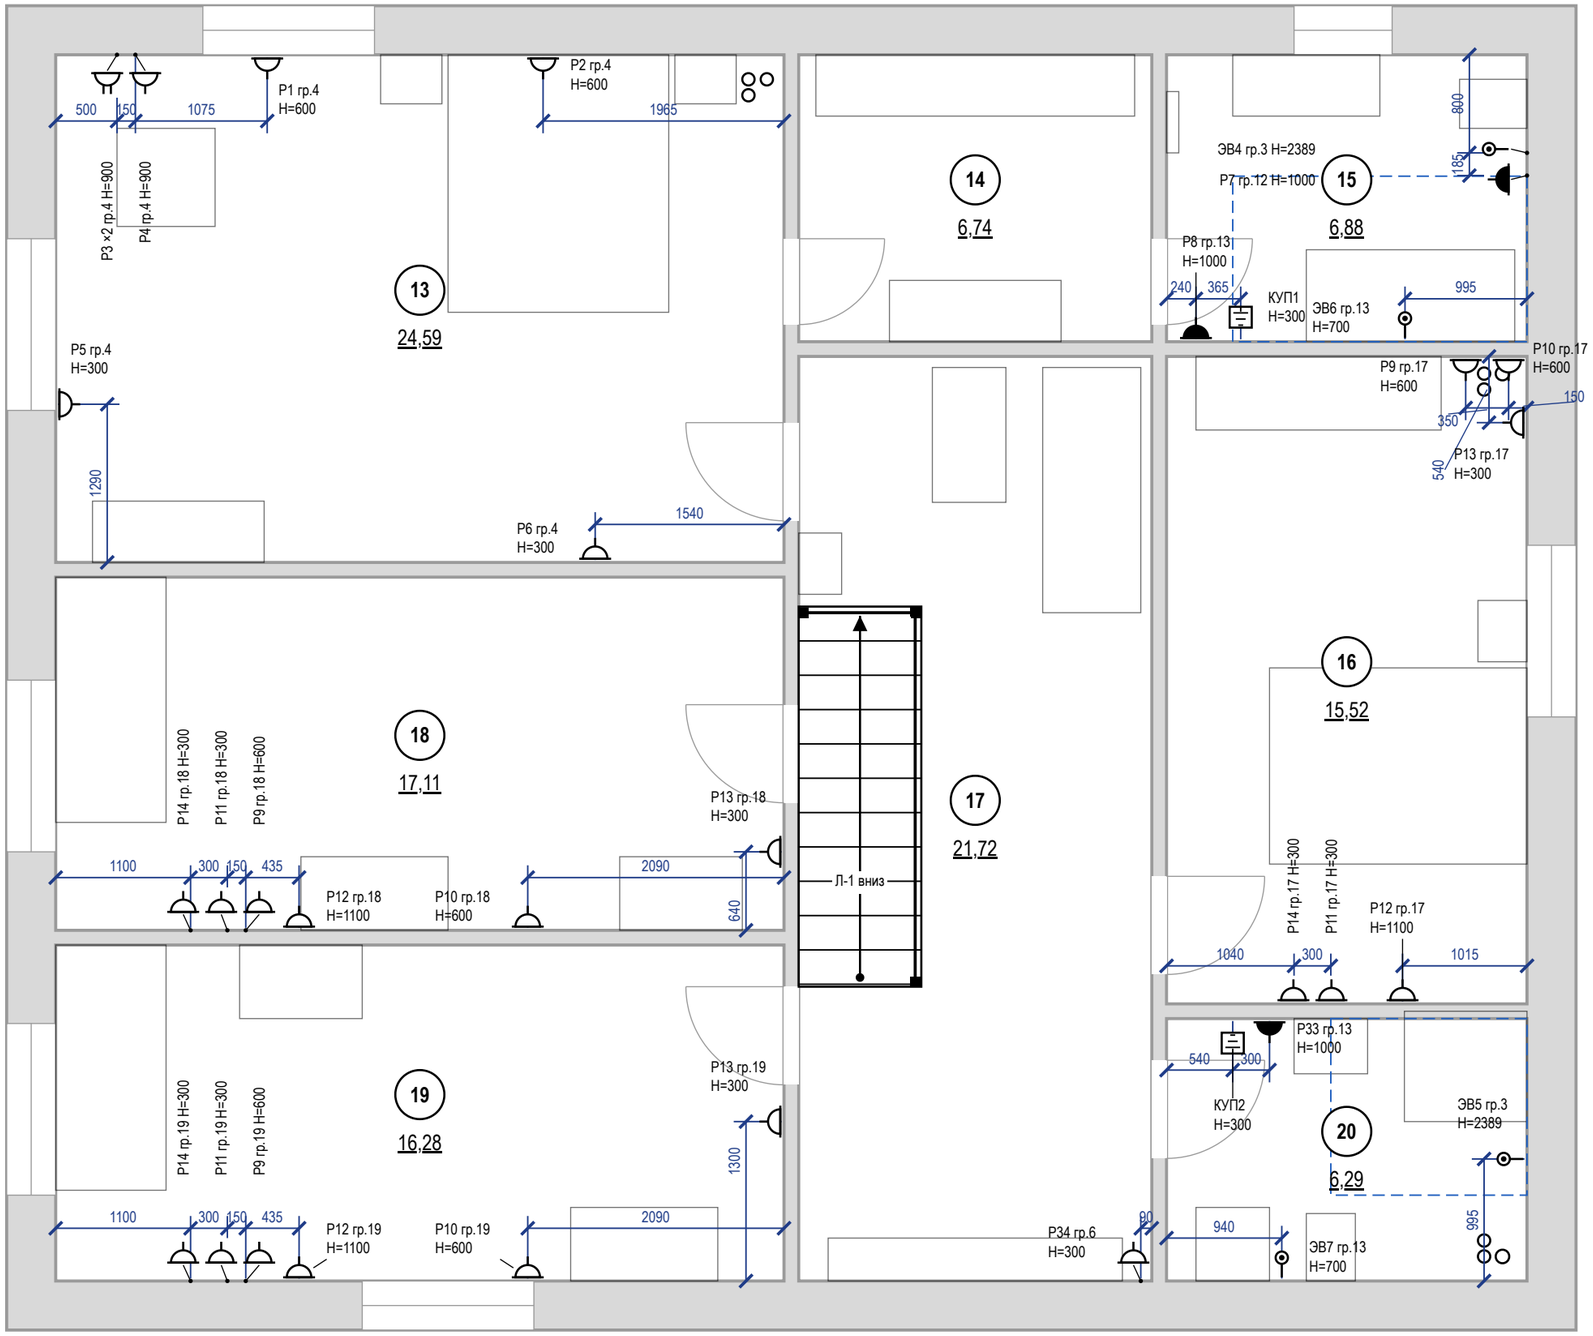

Условные обозначения


- розетка с заземляющим контактом; у знака — марка, ×N постов в рамке, гр. — группа щита, H — высота оси, мм
- то же, рамка на 2 поста (число черточек — число постов)
- розетка влагозащищённая IP44
- вывод кабеля для подключения прибора (без розетки), марка ЭВ
- КУП — коробка уравнивания потенциалов (ДСУП), проводник к шине PE щита
- знак разведён для читаемости: точка на стене — у выноски, привязка — до неё
- граница зоны 2 ванной (600 мм от ванны/поддона)
- мебель и сантехприборы — подложка
- стояк: К1 — канализация, В1 — ХВС, Т3 — ГВС
- (1) номер помещения, площадь м²

Примечания

1. За отметку 0,000 принят уровень чистого пола. Высоты H — от чистого пола до оси изделия; привязки — от чистовой грани стены до оси механизма (у рамки на несколько постов — до оси рамки).
2. Высота установки, не указанная на плане: розетки — 300 мм от чистого пола; выводы кабеля — по паспорту прибора.
3. Розетки в санузле — только вне зон 0–2 (ПУЭ 7.1.48, ГОСТ Р 50571.7.701-2024), IP44, через УЗО 30 мА.
4. Розеточные и мокрые линии — через УЗО или дифавтомат с током утечки не более 30 мА (ПУЭ 7.1.79); в санузле выполнить ДСУП (ПУЭ 7.1.87–7.1.88).
5. Кабель — медный, исполнение нг(A)-LS (ГОСТ 31565-2012); скрытая прокладка только горизонтально и вертикально, фактические трассы зафиксировать исполнительной схемой до закрытия отделкой.
6. Расчёт нагрузок, токов КЗ, селективности и сечений — по проекту ЭОМ организации с допуском СРО; лист задаёт состав, расположение и группы.
7. Электрический тёплый пол проектом не предусмотрен; при решении заказчика устроить — отдельный лист «План тёплых полов»: контуры с отступом 100 мм от стен и мебели без ножек, датчик в гофре, терморегулятор, своя группа щита через УЗО 30 мА.
8. Ведомости электроточек, изделий, светильников и расшифровка клавиш — лист «Ведомость электроточек и изделий».

	Лист	№ док.	Подпись	Дата	Проект: Дом 331 м²
Дизайнер	Кырлан А.С.			19.10.26	План розеток и электровыводов · Мансарда

Стадия	Лист	Листов
П	34	155

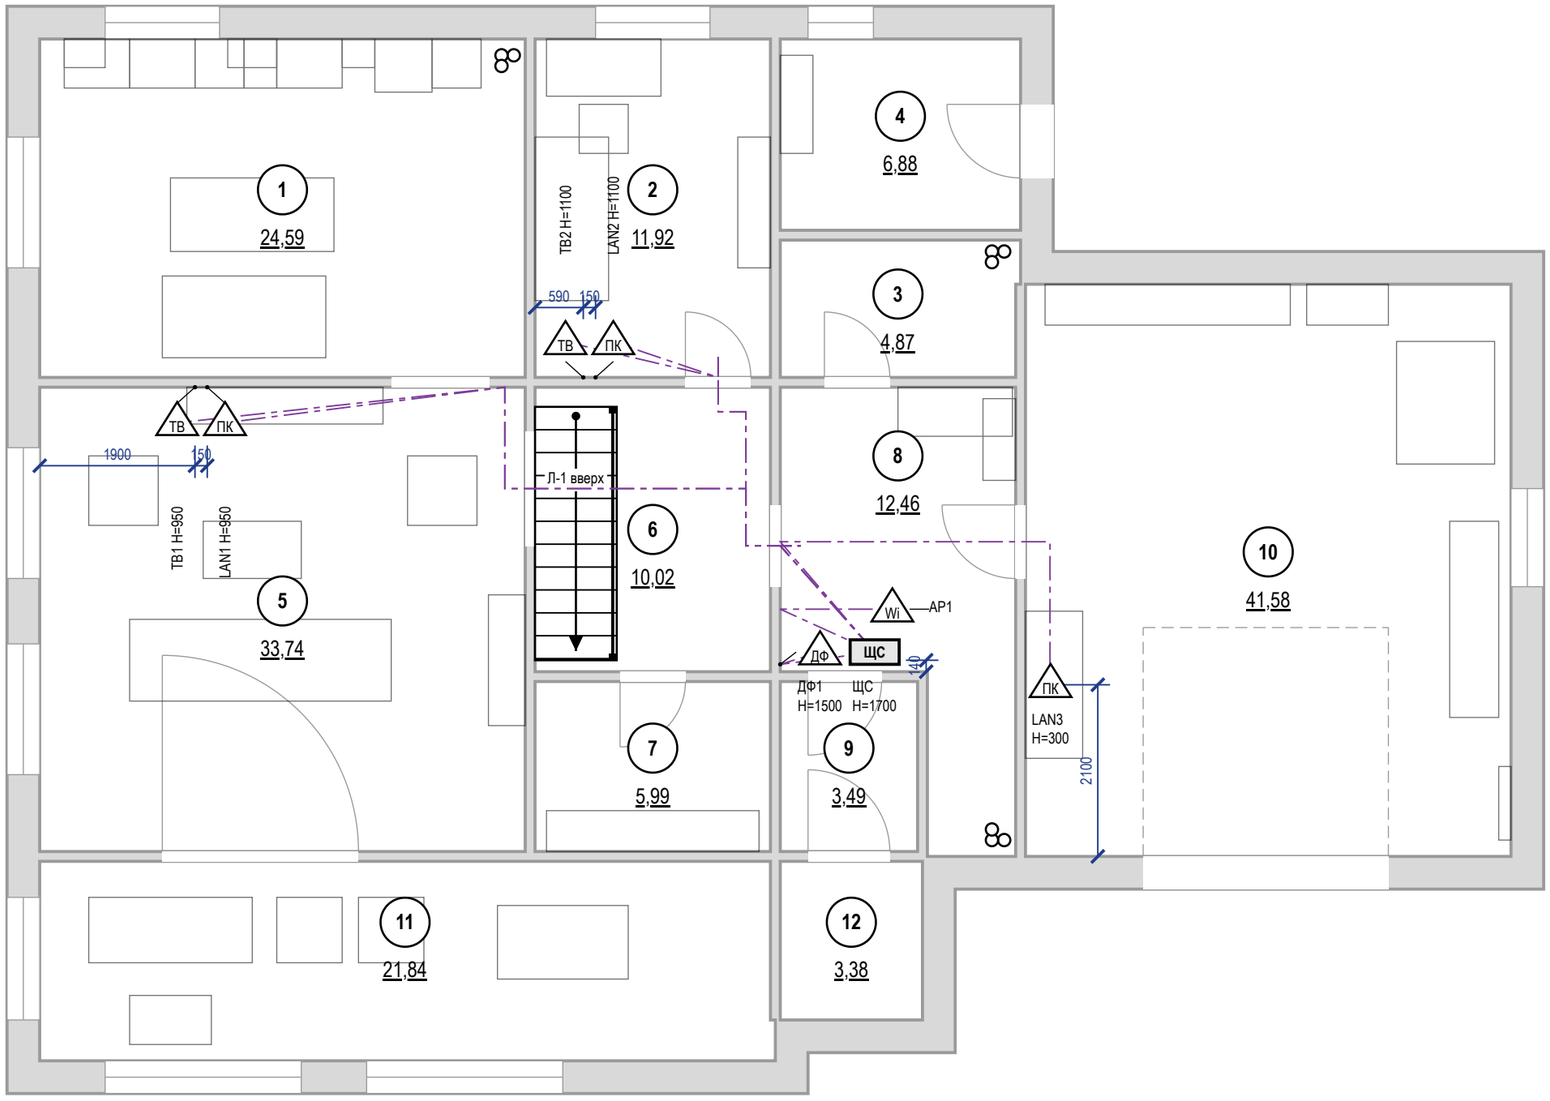


Примечания

1. За отметку 0,000 принят уровень чистого пола. Высоты Н — от чистого пола до оси изделия; привязки — от чистовой грани стены до оси механизма (у рамки на несколько постов — до оси рамки).
2. Высота установки, не указанная на плане: розетки LAN и ТВ — 300 мм от чистого пола.
3. Слаботочные кабели — отдельно от силовых: в своей трубе или лотке, при параллельной прокладке не ближе 100 мм к силовым, пересечения под прямым углом; каждую точку — отдельным кабелем от ЩС без скруток.
4. Трассы на листе — принципиальные; фактические зафиксировать исполнительной схемой до закрытия отделкой. Силовые линии, УЗО 30 мА, ДСУП, кабель нг(А)-LS — по листам розеток и щита.
5. Проект силовой части и расчёт токов КЗ — по проекту ЭОМ; слаботочная часть согласуется с провайдером и управляющей компанией (домофон, коллективное ТВ).

					Проект: Дом 331 м²
	Лист	№ док.	Подпись	Дата	План слаботочных сетей · 1-й этаж
Дизайнер	Кырлан А.С.			19.10.26	

Стадия	Лист	Листов
П	35	155

выпуск 18.10.2026 № ffc1f29499 · стр. 35 из 155

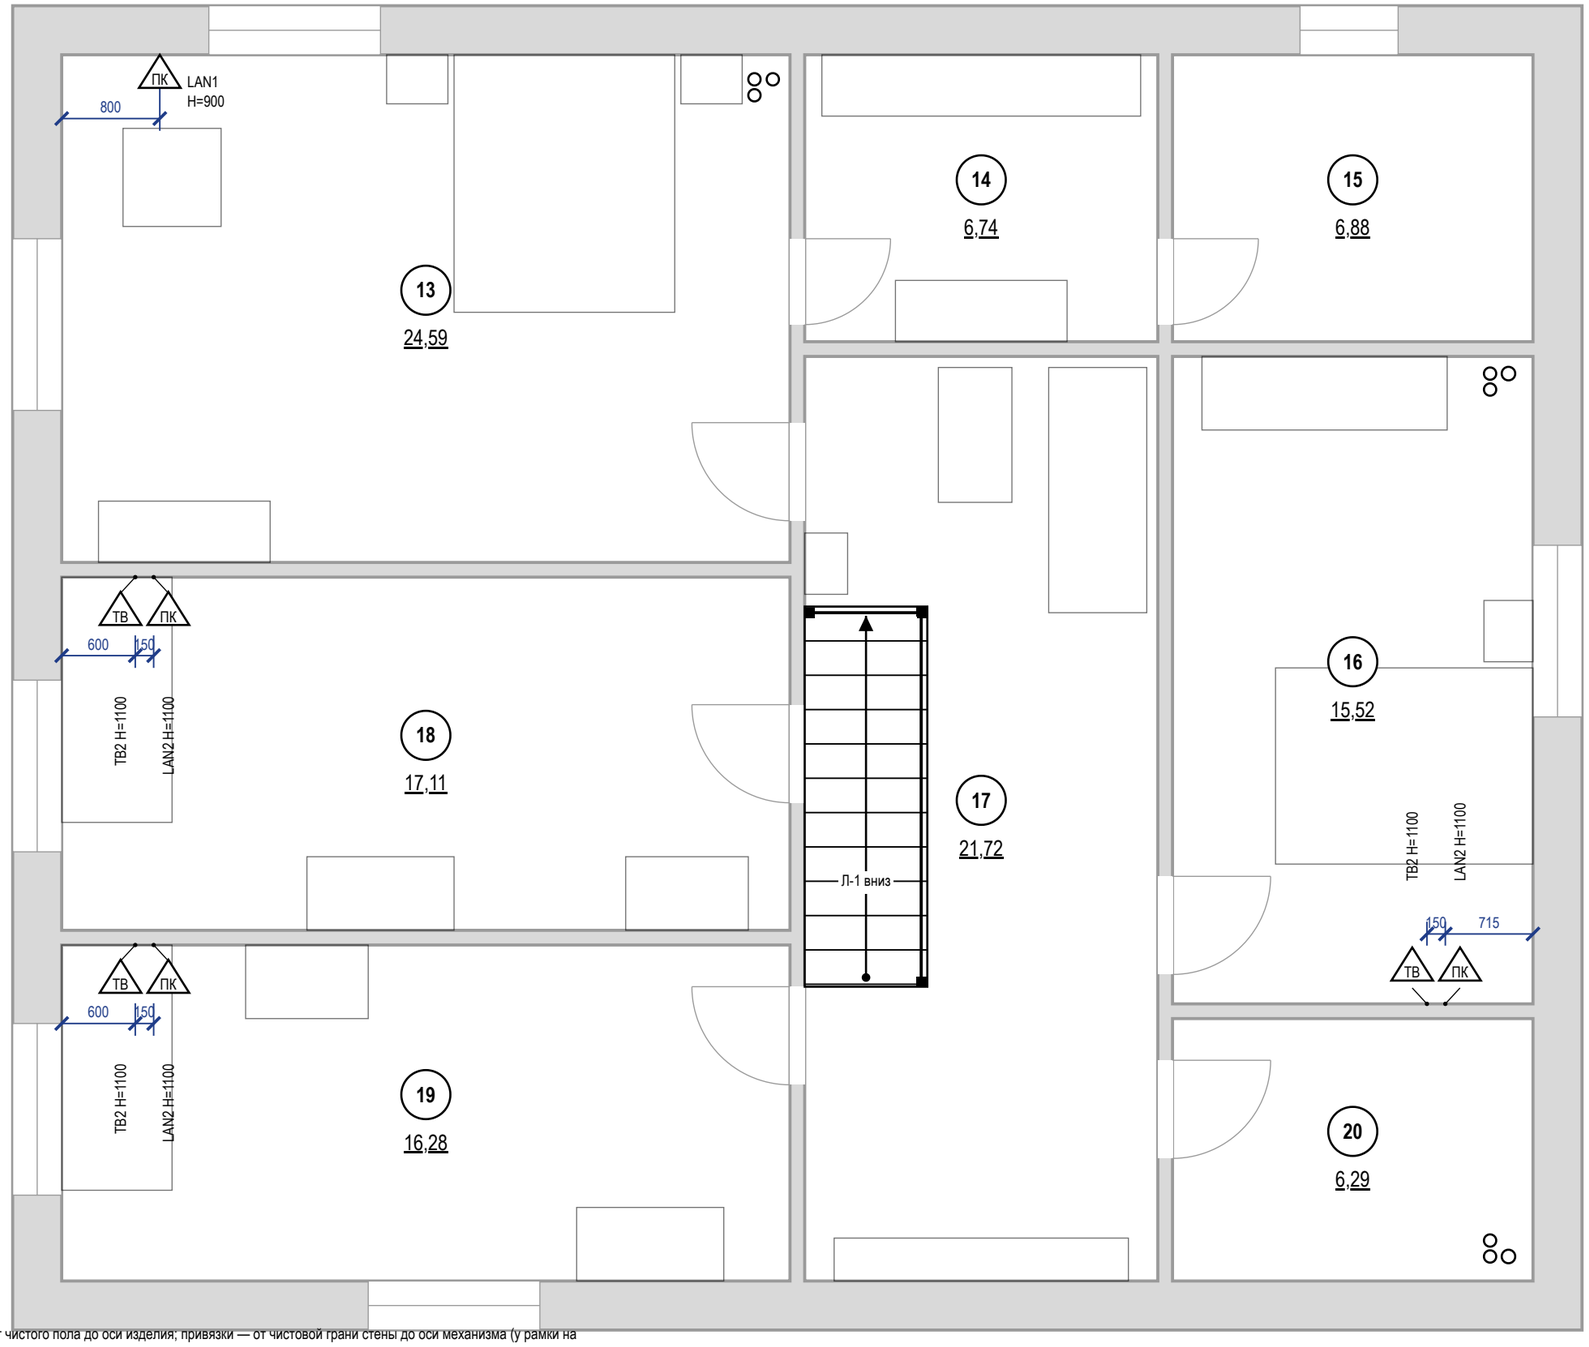


Примечания

1. За отметку 0,000 принят уровень чистого пола. Высоты H — от чистого пола до оси изделия; привязки — от чистовой грани стены до оси механизма (у рамки на несколько постов — до оси рамки).
2. Высота установки, не указанная на плане: розетки LAN и ТВ — 300 мм от чистого пола.
3. Слаботочные кабели — отдельно от силовых: в своей трубе или лотке, при параллельной прокладке не ближе 100 мм к силовым, пересечения под прямым углом; каждую точку — отдельным кабелем от ЩС без скруток.
4. Трассы на листе — принципиальные; фактические зафиксировать исполнительной схемой до закрытия отделкой. Силовые линии, УЗО 30 мА, ДСУП, кабель нг(А)-LS — по листам розеток и щита.
5. Проект силовой части и расчёт токов КЗ — по проекту ЭОМ; слаботочная часть согласуется с провайдером и управляющей компанией (домофон, коллективное ТВ).

					Проект: Дом 331 м²
	Лист	№ док.	Подпись	Дата	
Дизайнер	Кырлан А.С.			19.10.26	План слаботочных сетей · Мансарда

Стадия	Лист	Листов
П	36	155


выпуск 18.10.2026 № ffc1f29499 · стр. 36 из 155

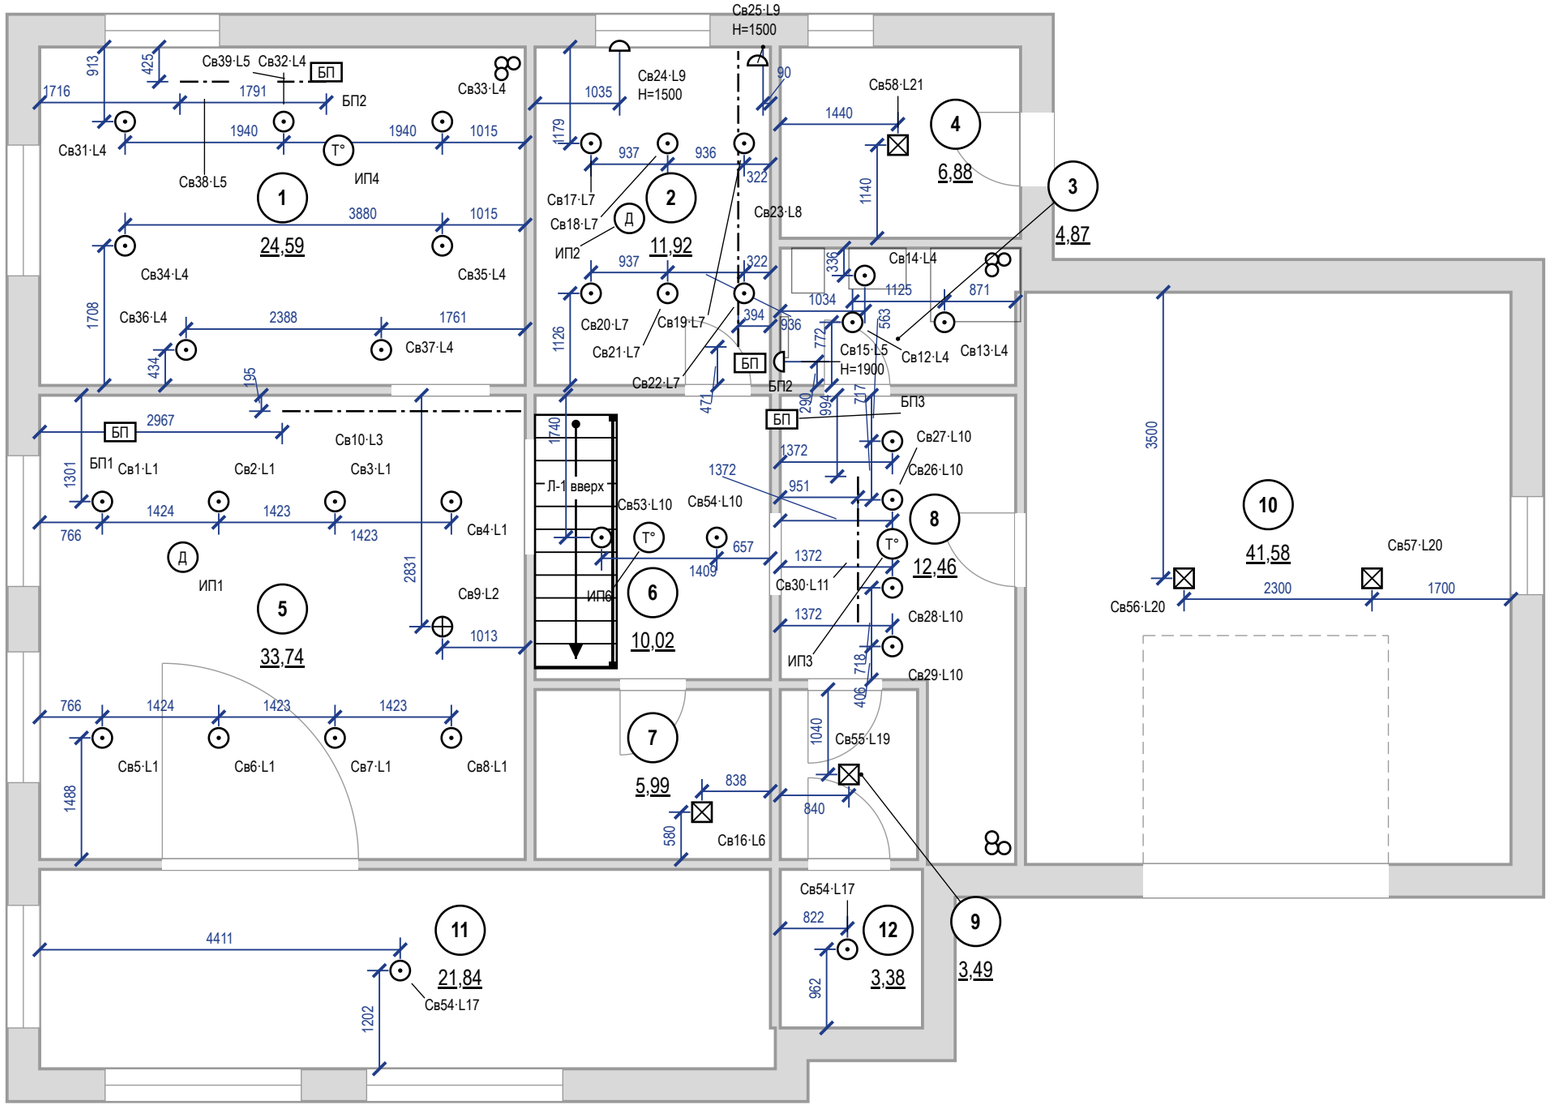

Примечания

1. За отметку 0,000 принят уровень чистого пола. Высоты H — от чистого пола до оси изделия; привязки — от чистовой грани стены до оси механизма (у рамки на несколько постов — до оси рамки).
2. Высота установки, не указанная на плане: светильники — на потолке; настенные — по отметке H у знака. Привязки — до оси светильника от чистовой грани стены, по рядам.
3. Освещённость: Ен — СанПиН 1.2.3685-21, табл. 5.52 (на полу); Ф треб. = Ен·S/(U·MF) при U = 0,5 и MF = 0,71 (СП 52.13330.2016, табл. 4.3) — оценка, не светотехнический расчёт. Декоративная подсветка в Ф не входит.
4. Во влажных помещениях — светильники не ниже IP44; в зонах 0–2 ванной — по ГОСТ Р 50571.7.701-2024 (зона 1 — IPX5).
5. Розеточные и мокрые линии — через УЗО или дифавтомат с током утечки не более 30 мА (ПУЭ 7.1.79); в санузле выполнить ДСУП (ПУЭ 7.1.87–7.1.88).
6. Кабель — медный, исполнение нг(A)-LS (ГОСТ 31565-2012); скрытая прокладка только горизонтально и вертикально, фактические трассы зафиксировать исполнительной схемой до закрытия отделкой.
7. Расчёт нагрузок, токов КЗ, селективности и сечений — по проекту ЭОМ организации с допуском СРО; лист задаёт состав, расположение и группы.
8. Ведомость светильников — лист «Ведомость электроточек и изделий».

					Проект: Дом 331 м²
	Лист	№ док.	Подпись	Дата	План освещения · 1-й этаж
Дизайнер	Кырлан А.С.			19.10.26	Стадия: П; Лист: 37; Листов: 155

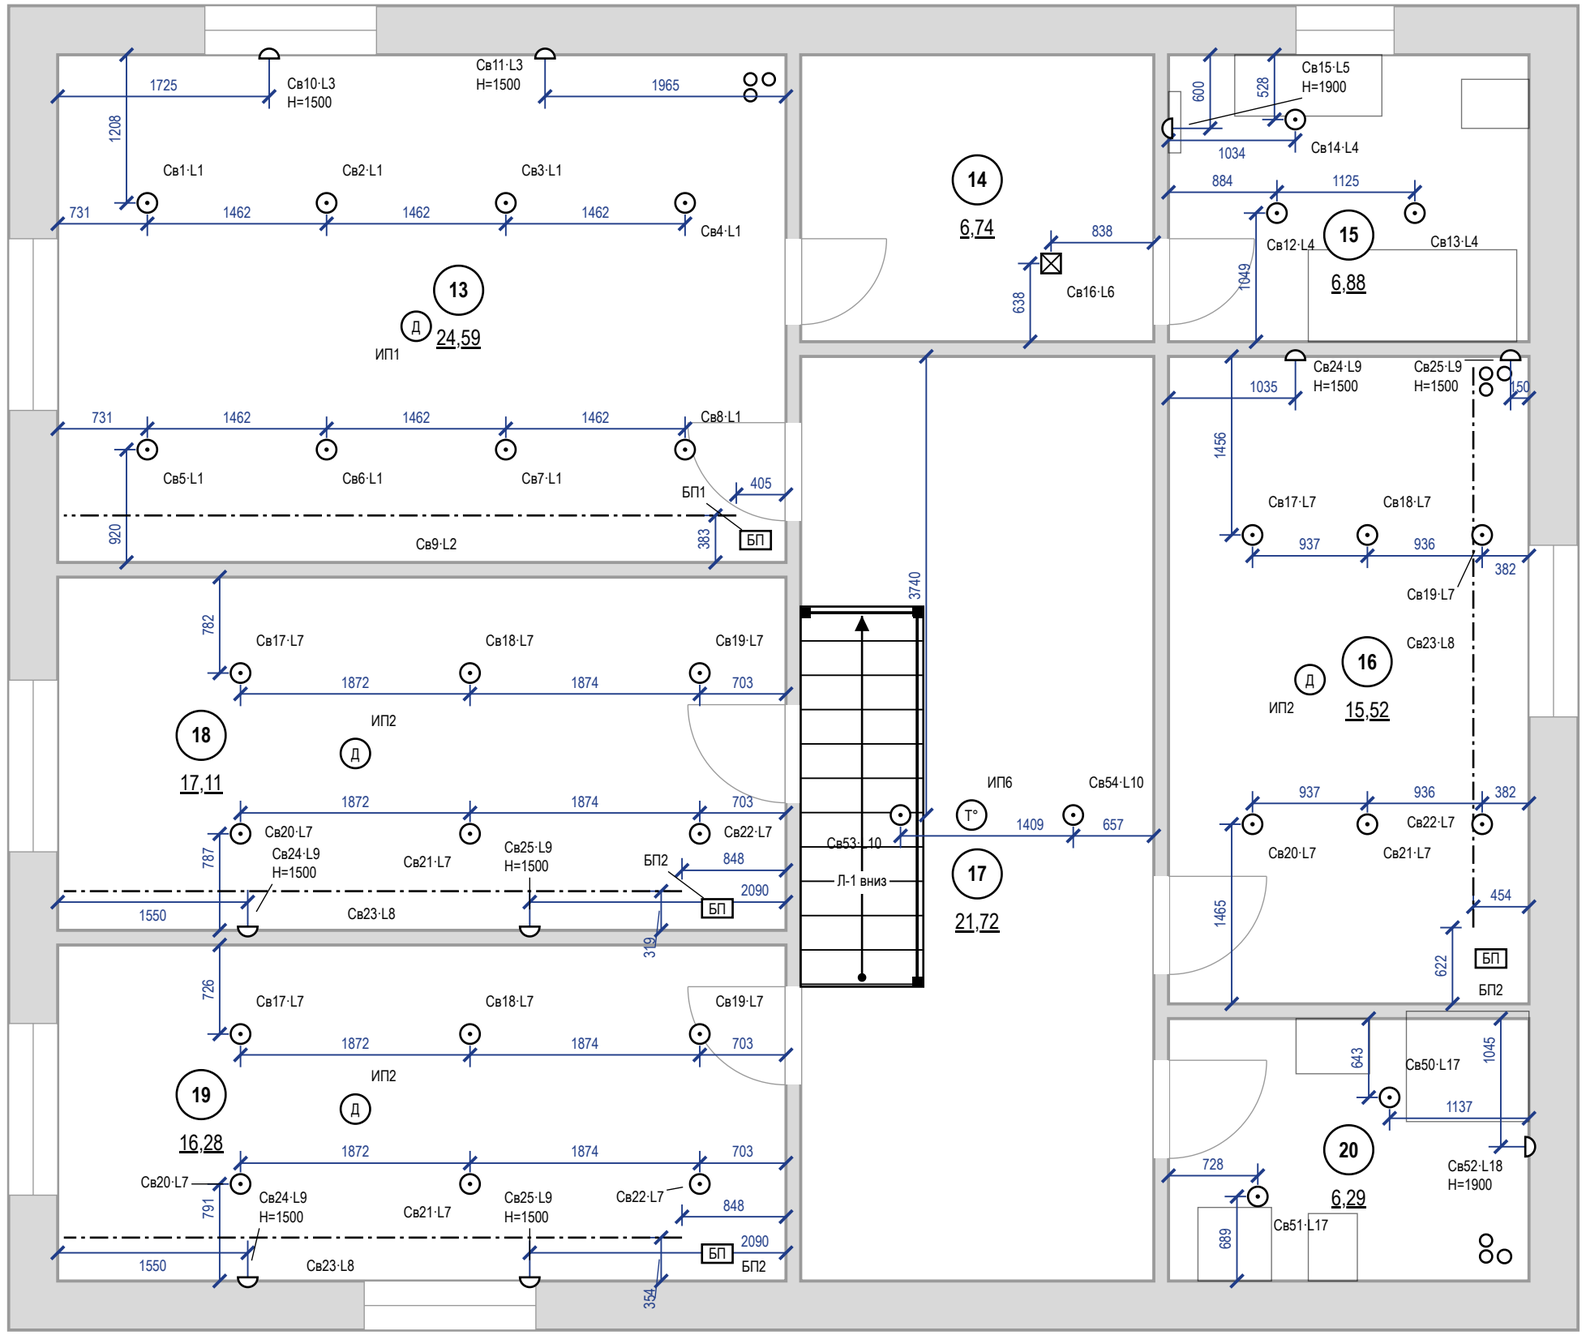

Примечания

1. За отметку 0,000 принят уровень чистого пола. Высоты Н — от чистого пола до оси изделия; привязки — от чистовой грани стены до оси механизма (у рамки на несколько постов — до оси рамки).
2. Высота установки, не указанная на плане: светильники — на потолке; настенные — по отметке Н у знака. Привязки — до оси светильника от чистовой грани стены, по рядам.
3. Освещённость: Ен — СанПиН 1.2.3685-21, табл. 5.52 (на полу); Ф треб. = Ен·S/(U·MF) при U = 0,5 и MF = 0,71 (СП 52.13330.2016, табл. 4.3) — оценка, не светотехнический расчёт. Декоративная подсветка в Ф не входит.
4. Во влажных помещениях — светильники не ниже IP44; в зонах 0–2 ванной — по ГОСТ Р 50571.7.701-2024 (зона 1 — IPX5).
5. Розеточные и мокрые линии — через УЗО или дифавтомат с током утечки не более 30 мА (ПУЭ 7.1.79); в санузле выполнить ДСУП (ПУЭ 7.1.87–7.1.88).
6. Кабель — медный, исполнение нг(A)-LS (ГОСТ 31565-2012); скрытая прокладка только горизонтально и вертикально, фактические трассы зафиксировать исполнительной схемой до закрытия отделкой.
7. Расчёт нагрузок, токов КЗ, селективности и сечений — по проекту ЭОМ организации с допуском СРО; лист задаёт состав, расположение и группы.
8. Ведомость светильников — лист «Ведомость электроточек и изделий».

	Лист	№ док.	Подпись	Дата
Дизайнер	Кырлан А.С.			19.10.26

Проект: Дом 331 м²

План освещения · Мансарда

Стадия	Лист	Листов
П	38	155

выпуск 18.10.2026 № ffc1f29499 · стр. 38 из 155

Спецификация светильников

Поз.	Марки	Наименование	Установка	Кол.	P, Вт	Σ P, Вт	Ф, лм	Тц, К	Ra	Угол, °	IP	Дим.	Группа	Пом.
1	Св1–Св8, Св31–Св37	Встраиваемый точечный	встраиваемый	15	12	180	1000	3000	90	—	20	—	L1, L4	1, 5
2	Св38, Св39	Линейный светильник	на поверхности	1,2 м	8	16	700	3000	90	—	20	—	L5	1
3	Св17–Св22	Встраиваемый точечный	встраиваемый	24	12	288	1050	2700	90	—	20	—	L7	2, 16, 18, 19
4	Св23	Лента светодиодная 24 В	в коробе, профиль с рассеивателем	49,2 м	9,6/м	472,3	900/м	2700	90	—	20	да	L8	2, 16, 18, 19
5	Св10, Св11, Св24, Св25	Настенный (бра)	на стене, H=1500	10	6	60	400	2700	90	60	20	да	L3, L9	2, 13, 16, 18, 19
6	Св12–Св14, Св51	Встраиваемый точечный	встраиваемый	7	6	42	500	3000	90	—	44	—	L4, L17	3, 15, 20
7	Св15, Св52	Настенный светильник над зеркалом, драйвер встроен	над зеркалом, H=1900	3	8	24	600	3000	90	—	44	—	L5, L18	3, 15, 20
8	Св16, Св55, Св58	Потолочный накладной	на потолке	4	10	40	900	3000	90	—	20	—	L6, L19, L21	4, 7, 9, 14
9	Св9	Подвесной	подвес, низ H=1600	1	15	15	1200	2700	90	—	20	—	L2	5
10	Св10	Лента светодиодная 24 В	в коробе, профиль с рассеивателем	5 м	9,6/м	48	900/м	2700	90	—	20	да	L3	5
11	Св26–Св29, Св53, Св54	Встраиваемый точечный	встраиваемый	8	7	56	600	3000	90	—	20	—	L10	6, 8, 17
12	Св30	Лента светодиодная 24 В	в коробе, профиль с рассеивателем, датчик движения	1,8 м	4,8/м	8,6	150/м	2700	90	—	20	нет	L11	8
13	Св56, Св57	Потолочный накладной	на потолке	2	24	48	2500	3000	90	—	20	—	L20	10
14	Св54	Встраиваемый точечный	встраиваемый	2	9	18	800	3000	90	—	44	—	L17	11, 12
15	Св1–Св8	Встраиваемый точечный	встраиваемый	8	12	96	1000	2700	90	—	20	—	L1	13
16	Св9	Лента светодиодная 24 В	в коробе, профиль с рассеивателем	15,5 м	9,6/м	148,8	900/м	2700	90	—	20	да	L2	13
17	Св50	Встраиваемый точечный	встраиваемый	1	7	7	600	3000	90	—	44	—	L17	20
		Итого		**85 шт + 72,7 м**		**1567,8**								

LED-ленты, линейные светильники и блоки питания

Марка	Пом.	L, м	U, В	Вт/м	Σ P, Вт	БП	P БП, Вт	Загр., %	Питание	Доступ к БП
Св38	1	0,6	24	—	8	БП2	200	244	встроенный ввод	люк 300×300 в коробе У1 у окна
Св39	1	0,6	24	—	8	БП2	200	244	встроенный ввод	люк 300×300 в коробе У1 у окна
Св23	2	12,3	24	9,6	118,1	БП2	200	244	с двух концов	люк 300×300 в коробе У1 у окна
Св10	5	5	24	9,6	48	БП1	200	98	с одного конца	люк 300×300 в коробе У1 у входа
Св30	8	1,8	24	4,8	8,6	БП3	20	43	с одного конца	в шкафу М16, верхняя полка
Св9	13	15,5	24	9,6	148,8	БП1	200	98	с двух концов	люк 300×300 в коробе У1 у входа
Св23	16	12,3	24	9,6	118,1	БП2	200	244	с двух концов	люк 300×300 в коробе У1 у окна
Св23	18	12,3	24	9,6	118,1	БП2	200	244	с двух концов	люк 300×300 в коробе У1 у окна
Св23	19	12,3	24	9,6	118,1	БП2	200	244	с двух концов	люк 300×300 в коробе У1 у окна

Сценарии освещения

Пом.	Сценарий	Группы и уровни, %	Чем включается
2	Вечер	L7 споты — 0; L8 подсветка короба — 100; L9 бра — 100	S4, S5, S6
5	Вечер	L1 общий свет (споты) — 0; L2 подвес над обеденным столом — 100; L3 лента в карнизе (диммер) — 50	S1, S2, S2 светорегулятор, S3
5	Гости	L1 общий свет (споты) — 100; L2 подвес над обеденным столом — 100; L3 лента в карнизе (диммер) — 100	S1, S2, S2 светорегулятор, S3
5	Кино	L1 общий свет (споты) — 0; L2 подвес над обеденным столом — 0; L3 лента в карнизе (диммер) — 20	S2, S2 светорегулятор, S3
5	Уборка	L1 общий свет (споты) — 100; L2 подвес над обеденным столом — 100; L3 лента в карнизе (диммер) — 0	S1, S2, S3
13	Вечер	L1 общий свет (споты) — 0; L2 подвес над обеденным столом — 100; L3 лента в карнизе (диммер) — 100	S1, S2, S2 светорегулятор, S3
13	Уборка	L1 общий свет (споты) — 100; L2 подвес над обеденным столом — 100; L3 лента в карнизе (диммер) — 0	S1, S2, S3
16	Вечер	L7 споты — 0; L8 подсветка короба — 100; L9 бра — 100	S4, S5, S6
18	Вечер	L7 споты — 0; L8 подсветка короба — 100; L9 бра — 100	S4, S5, S6
19	Вечер	L7 споты — 0; L8 подсветка короба — 100; L9 бра — 100	S4, S5, S6

Слои света

общий — равномерный свет помещения, по норме освещённости

рабочий — местный свет задачи: столешница, зеркало, чтение у кровати


акцентный — подсветка потолка, стен и ниш; не входит в поток общего света

ночной — путь спальня → санузел: не выше 2700 K, малая яркость, датчик движения

Примечания

1. Позиции и марки Св — те же, что на плане освещения (лист «План освещения») и в ведомости светильников (лист «Ведомость электроточек и изделий»); группы L — по плану выключателей (лист «План выключателей»).
2. Модели светильников не назначены: подбор по графам спецификации — поток, Тц, Ra, угол, IP и диммирование не хуже указанных, мощность не больше. IP 20 — сухие помещения.
3. Длина LED-ленты в карнизе — по линии карниза плана потолков (лист «План потолков»); Σ P = Вт/м × длина. Блок питания загружен не больше чем на 80 %; лента 24 В длиннее 10 м питается с двух концов; доступ к блоку питания — люк ревизии 300×300 мм или место, указанное в таблице.
4. Сценарии: уровень — доля максимальной яркости группы, %; 0 — группа выключена. Уровень ниже 100 % — только у групп на светорегуляторе (задний фронт, ТЕ) с диммируемыми драйверами и блоками питания.
5. Мощность и поток — по паспортам принятых изделий, Σ P — установленная мощность освещения. Оценка освещённости — на плане освещения; это не светотехнический расчёт.
6. Не поместилось строк таблиц: 20 — продолжение выпустить отдельным листом.

					Проект: Дом 331 м²	
	Лист	№ док.	Подпись	Дата		
Дизайнер	Кырлан А.С.			19.10.26	Спецификация светильников и сценарии освещения	Стадия: П; Лист: 39; Листов: 155

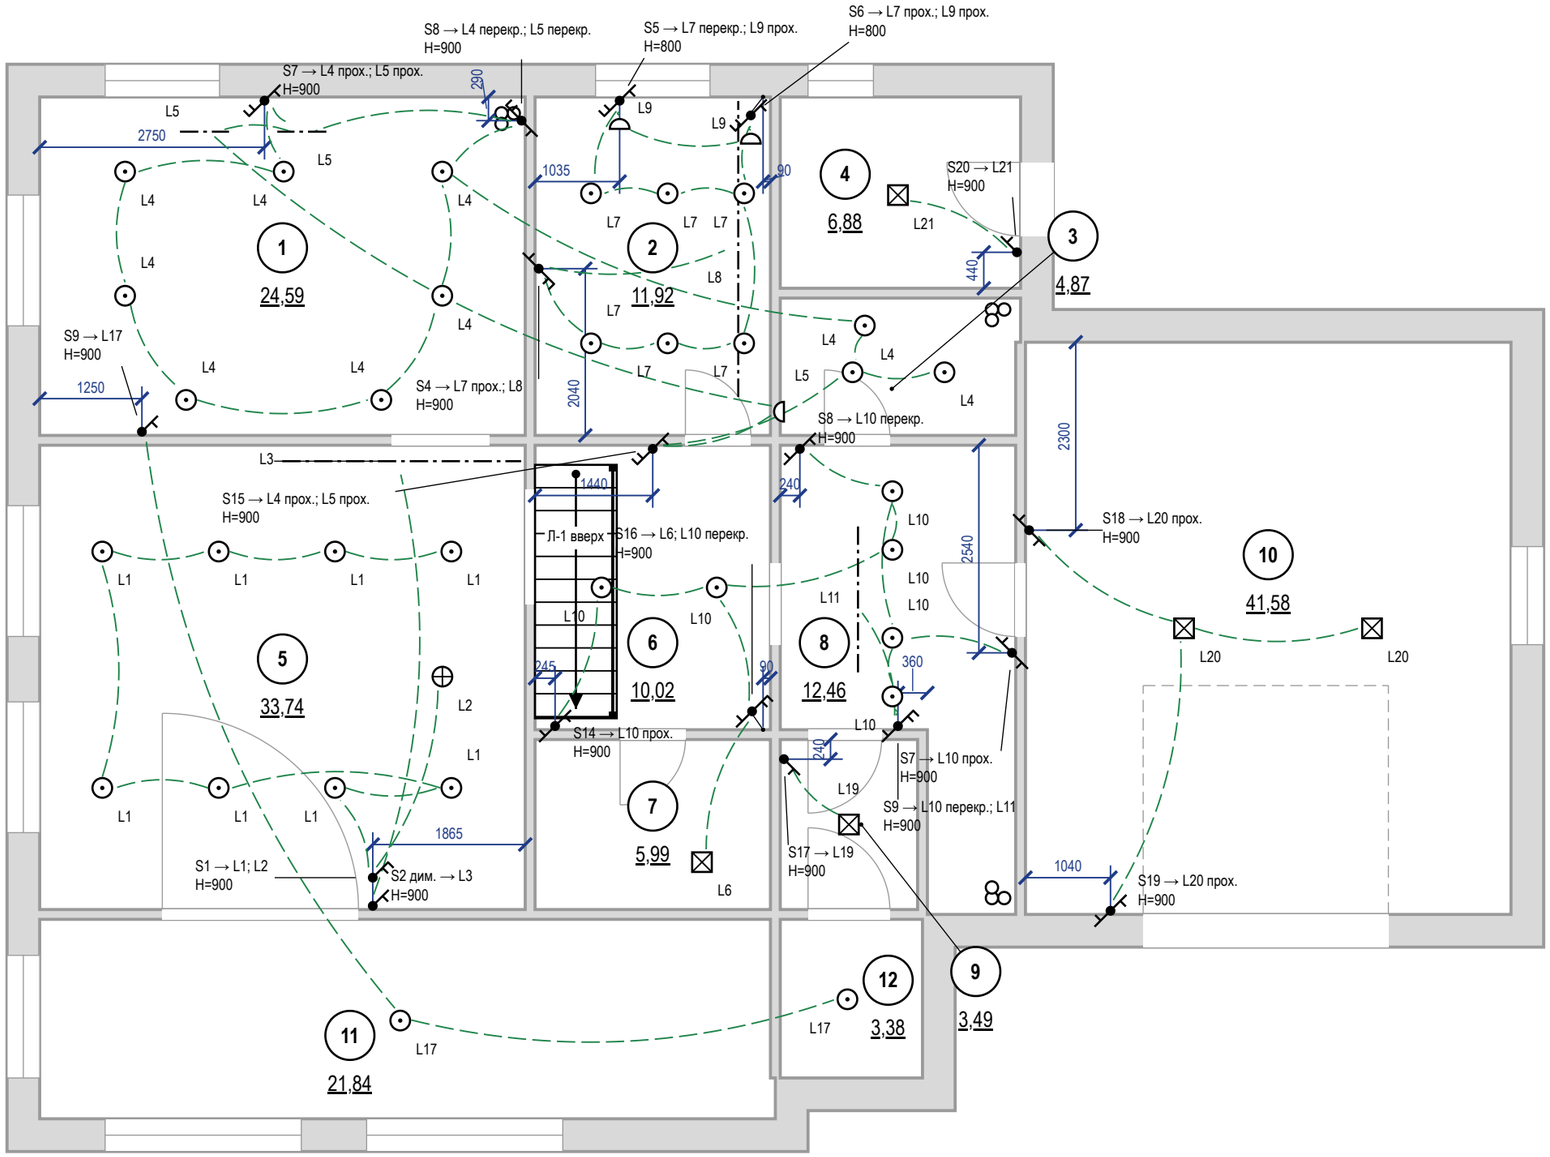


Примечания

1. За отметку 0,000 принят уровень чистого пола. Высоты H — от чистого пола до оси изделия; привязки — от чистовой грани стены до оси механизма (у рамки на несколько постов — до оси рамки).
2. Высота установки, не указанная на плане: выключатели — 900 мм от чистого пола, со стороны дверной ручки (ПУЭ 7.1.51).
3. Линии связи показывают, какой выключатель какую группу L включает; это не трасса кабеля. Трасса — принципиальная, фактическую зафиксировать исполнительной схемой.
4. Группы из нескольких мест (L4 — S7, S8, S15; L5 — S7, S8, S15; L7 — S4, S5, S6; L9 — S5, S6; L10 — S7, S8, S9, S14, S16; L20 — S18, S19): на крайних местах проходные клавиши, на промежуточных — перекрёстные; механизмы — в ведомости изделий.
5. Светорегулятор — по заднему фронту (для LED-драйверов), совместимость с драйверами проверить до закупки.
6. Розеточные и мокрые линии — через УЗО или дифавтомат с током утечки не более 30 мА (ПУЭ 7.1.79); в санузле выполнить ДСУП (ПУЭ 7.1.87–7.1.88).
7. Кабель — медный, исполнение нг(A)-LS (ГОСТ 31565-2012); скрытая прокладка только горизонтально и вертикально, фактические трассы зафиксировать исполнительной схемой до закрытия отделкой.
8. Расчёт нагрузок, токов КЗ, селективности и сечений — по проекту ЭОМ организации с допуском СРО; лист задаёт состав, расположение и группы.
9. Расшифровка клавиш и ведомость изделий — лист «Ведомость электроточек и изделий».

					Проект: Дом 331 м²
	Лист	№ док.	Подпись	Дата	Управление светильниками · 1-й этаж
Дизайнер	Кырлан А.С.			19.10.26	

Стадия	Лист	Листов
П	40	155

выпуск 18.10.2026 № ffc1f29499 · стр. 40 из 155

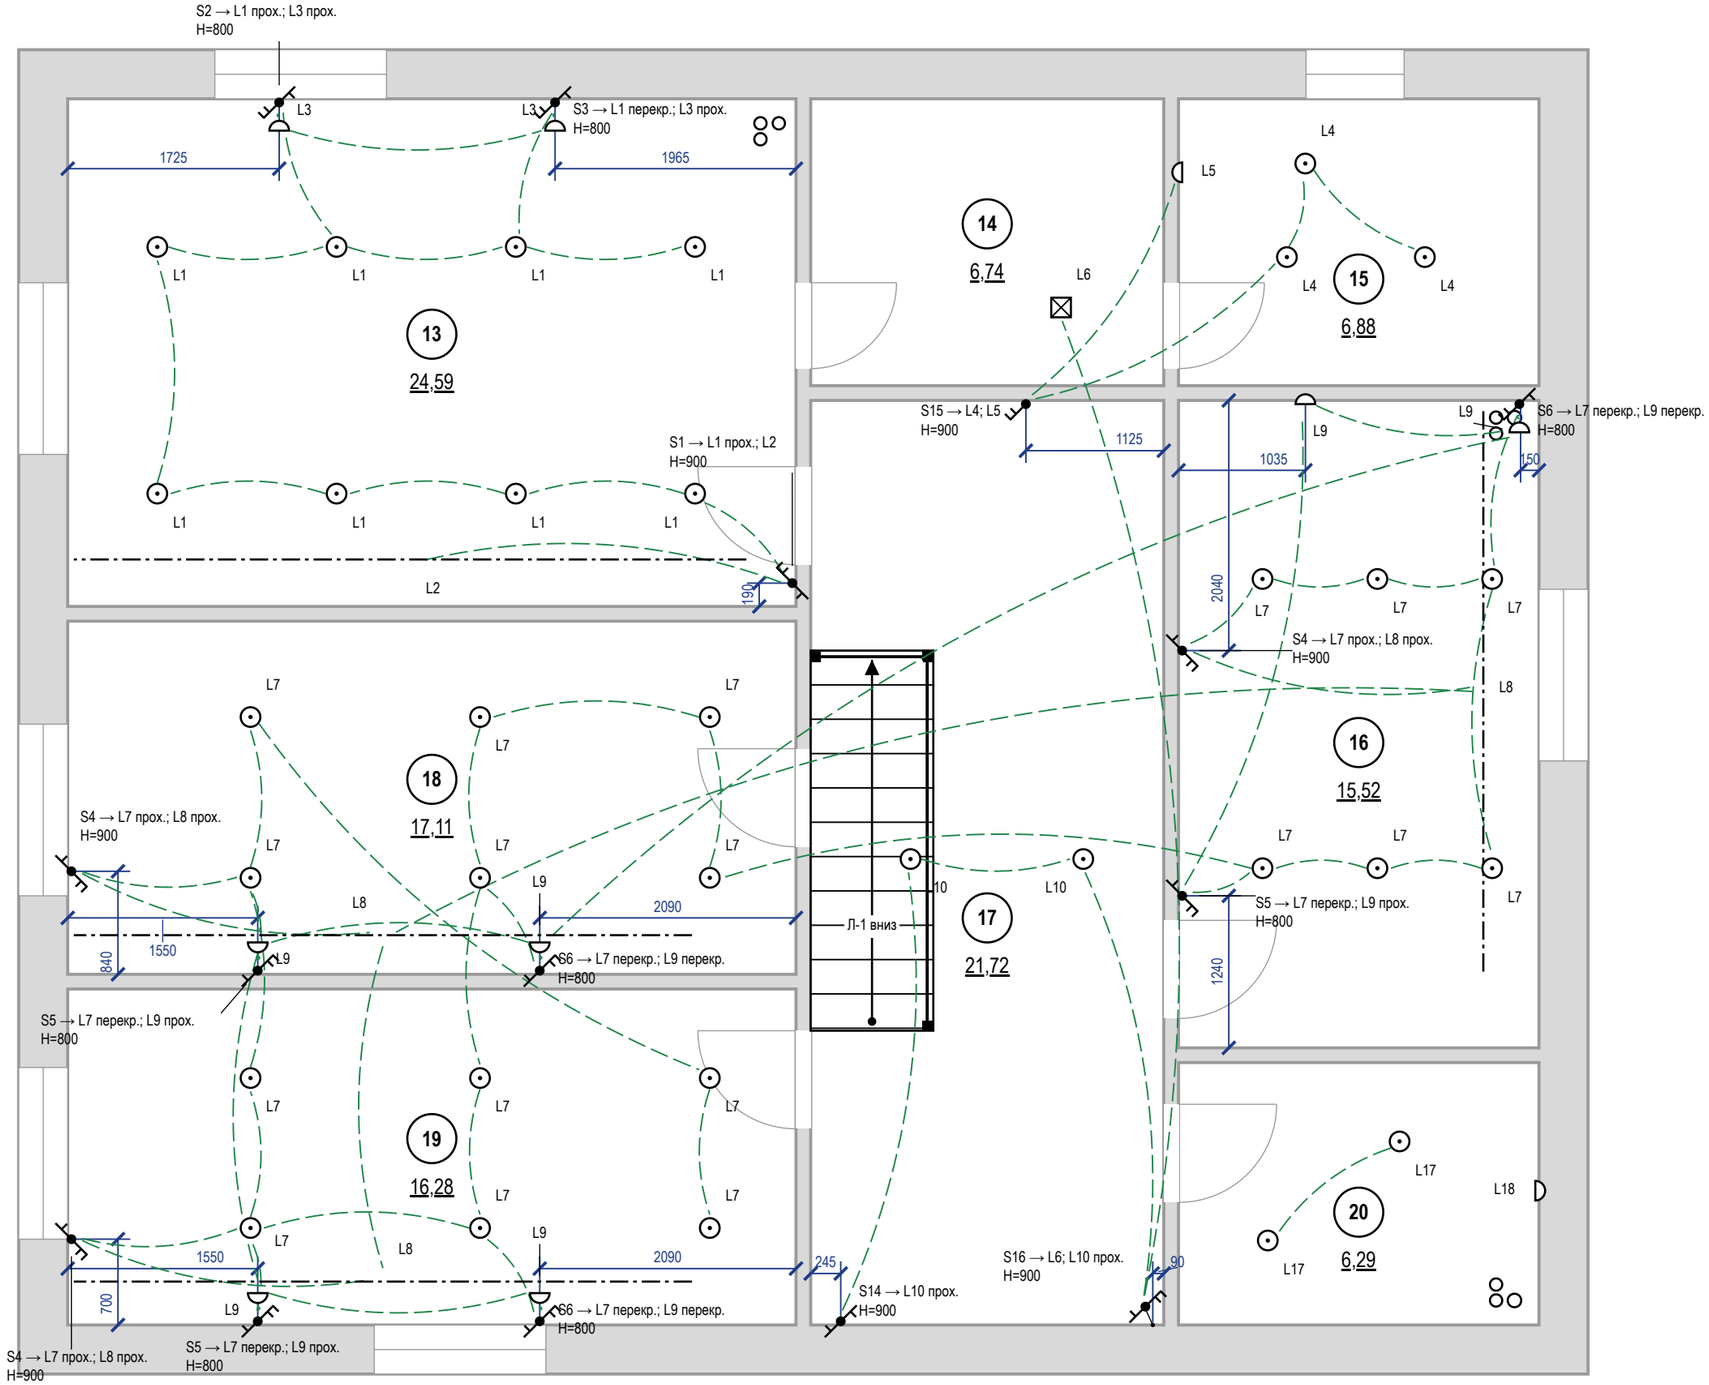


Примечания

1. За отметку 0,000 принят уровень чистого пола. Высоты H — от чистого пола до оси изделия; привязки — от чистовой грани стены до оси механизма (у рамки на несколько постов — до оси рамки).
2. Высота установки, не указанная на плане: выключатели — 900 мм от чистого пола, со стороны дверной ручки (ПУЭ 7.1.51).
3. Линии связи показывают, какой выключатель какую группу L включает; это не трасса кабеля. Трасса — принципиальная, фактическую зафиксировать исполнительной схемой.
4. Группы из нескольких мест (L1 — S1, S2, S3; L3 — S2, S3; L7 — S4, S4, S4, S5, S5, S5, S6, S6, S6; L8 — S4, S4, S4; L9 — S5, S5, S5, S6, S6, S6; L10 — S14, S16): на крайних местах проходные клавиши, на промежуточных перекрёстные; механизмы — в ведомости изделий.
5. Розеточные и мокрые линии — через УЗО или дифавтомат с током утечки не более 30 мА (ПУЭ 7.1.79); в санузле выполнить ДСУП (ПУЭ 7.1.87–7.1.88).
6. Кабель — медный, исполнение нг(A)-LS (ГОСТ 31565-2012); скрытая прокладка только горизонтально и вертикально, фактические трассы зафиксировать исполнительной схемой до закрытия отделкой.
7. Расчёт нагрузок, токов КЗ, селективности и сечений — по проекту ЭОМ организации с допуском СРО; лист задаёт состав, расположение и группы.
8. Группы без выключателя: L17, L18 — назначить управление до монтажа.
9. Расшифровка клавиш и ведомость изделий — лист «Ведомость электроточек и изделий».

					Проект: Дом 331 м²
	Лист	№ док.	Подпись	Дата	Управление светильниками · Мансарда
Дизайнер	Кырлан А.С.			19.10.26	

Стадия	Лист	Листов
П	41	155

выпуск 18.10.2026 № ffc1f29499 · стр. 41 из 155

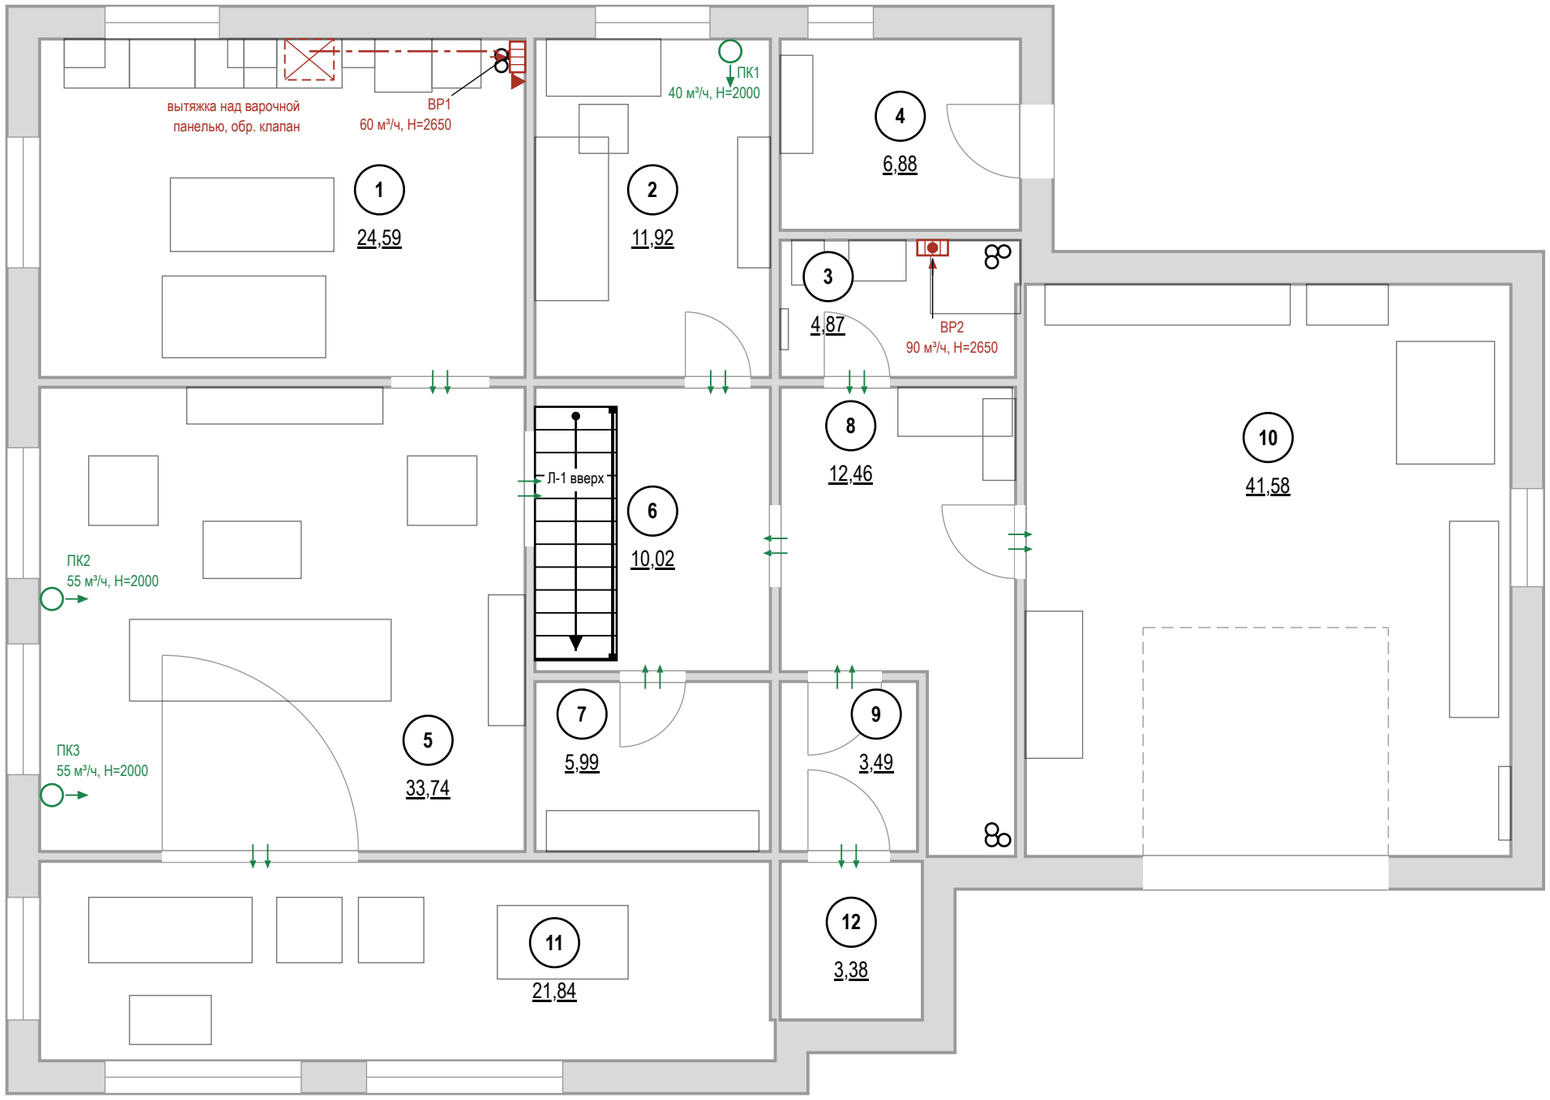

Условные обозначения

- стояк: К1 — канализация, В1 — ХВС, Т3 ГВС
- номер помещения, площадь м²
- вытяжная решётка в вентканал: марка, расход м³/ч, Н центра от чистого пола
- вытяжная решётка с бытовым вентилятором и обратным клапаном: марка, расход, Н
- приточный клапан (КИВ) в наружной стене: марка, расход, Н центра
- переток: зазор под полотном или переточная решётка
- кухонная вытяжка над варочной панелью
- воздуховод кухонной вытяжки в коробе под потолком
- отдельный вход воздуховода в вентканал, обратный клапан

Воздухообмен, м³/ч

№	Помещение	Выт. норма	Выт. проект	Прит. норма	Прит. проект	Устройства
1	Кухня-столовая	60	60			ВР1
2	Кабинет-гостевая			36	40	ПК1
3	Санузел 1 этажа	50	90			ВР2
4	Котельная	4				переток
5	Гостиная			102	110	ПК2, ПК3
7	Кладовая	3				переток
10	Гараж	23				переток
	Итого	**140**	**150**	**120**	**150**	

Воздухообмен квартиры — по большей из сумм притока и вытяжки: норма 140 м³/ч, проект 150 м³/ч.
Вытяжка не меньше притока — баланс сведён.


Примечания

1. Расчёт систем ОВ и подбор оборудования — проектная организация с допуском СРО; лист даёт места, трассы и привязки.
2. Нормы вытяжки — СП 54.13330.2022 (Изм. 1, 2), табл. 7.1: кухня с электроплитой 60 м³/ч, с газовой 100; ванная и совмещённый санузел 50; уборная 25; гардеробная 0,2 ч⁻¹. Приток в жилые — 3 м³/ч на 1 м² (менее 20 м² общей площади на человека), иначе 30 м³/ч на человека.
3. Вентканалы и шахты не сужать, не переносить и не закрывать; вентилятор и кухонная вытяжка — через обратный клапан, без перекрытия естественной тяги.
4. Проектные расходы — не ниже нормы, вытяжка сведена с притоком вентиляторами мокрых помещений. Клапаны — в простенке у окна, центр 2000 мм, не над кроватью, не ближе 300 мм к стоякам отопления; типоразмер — на расход.
5. Кухонная вытяжка в воздухообмен не включена: воздуховод не менее Ø125 в коробе, вход в канал отдельный.
6. Переток — зазор под полотнами межкомнатных дверей или переточная решётка.
7. Кондиционирование заданием не предусмотрено; при установке трассы фреона и дренажа (не менее 40 мм/м, в К1 через сифон) и питание заложить до черновых работ.
8. Привязки оборудования — по паспортам приобретённых моделей, до черновых работ.

					Проект: Дом 331 м²
	Лист	№ док.	Подпись	Дата	План вентиляции · 1-й этаж
Дизайнер	Кырлан А.С.			19.10.26	

Стадия	Лист	Листов
П	42	155

выпуск 18.10.2026 № ffc1f29499 · стр. 42 из 155

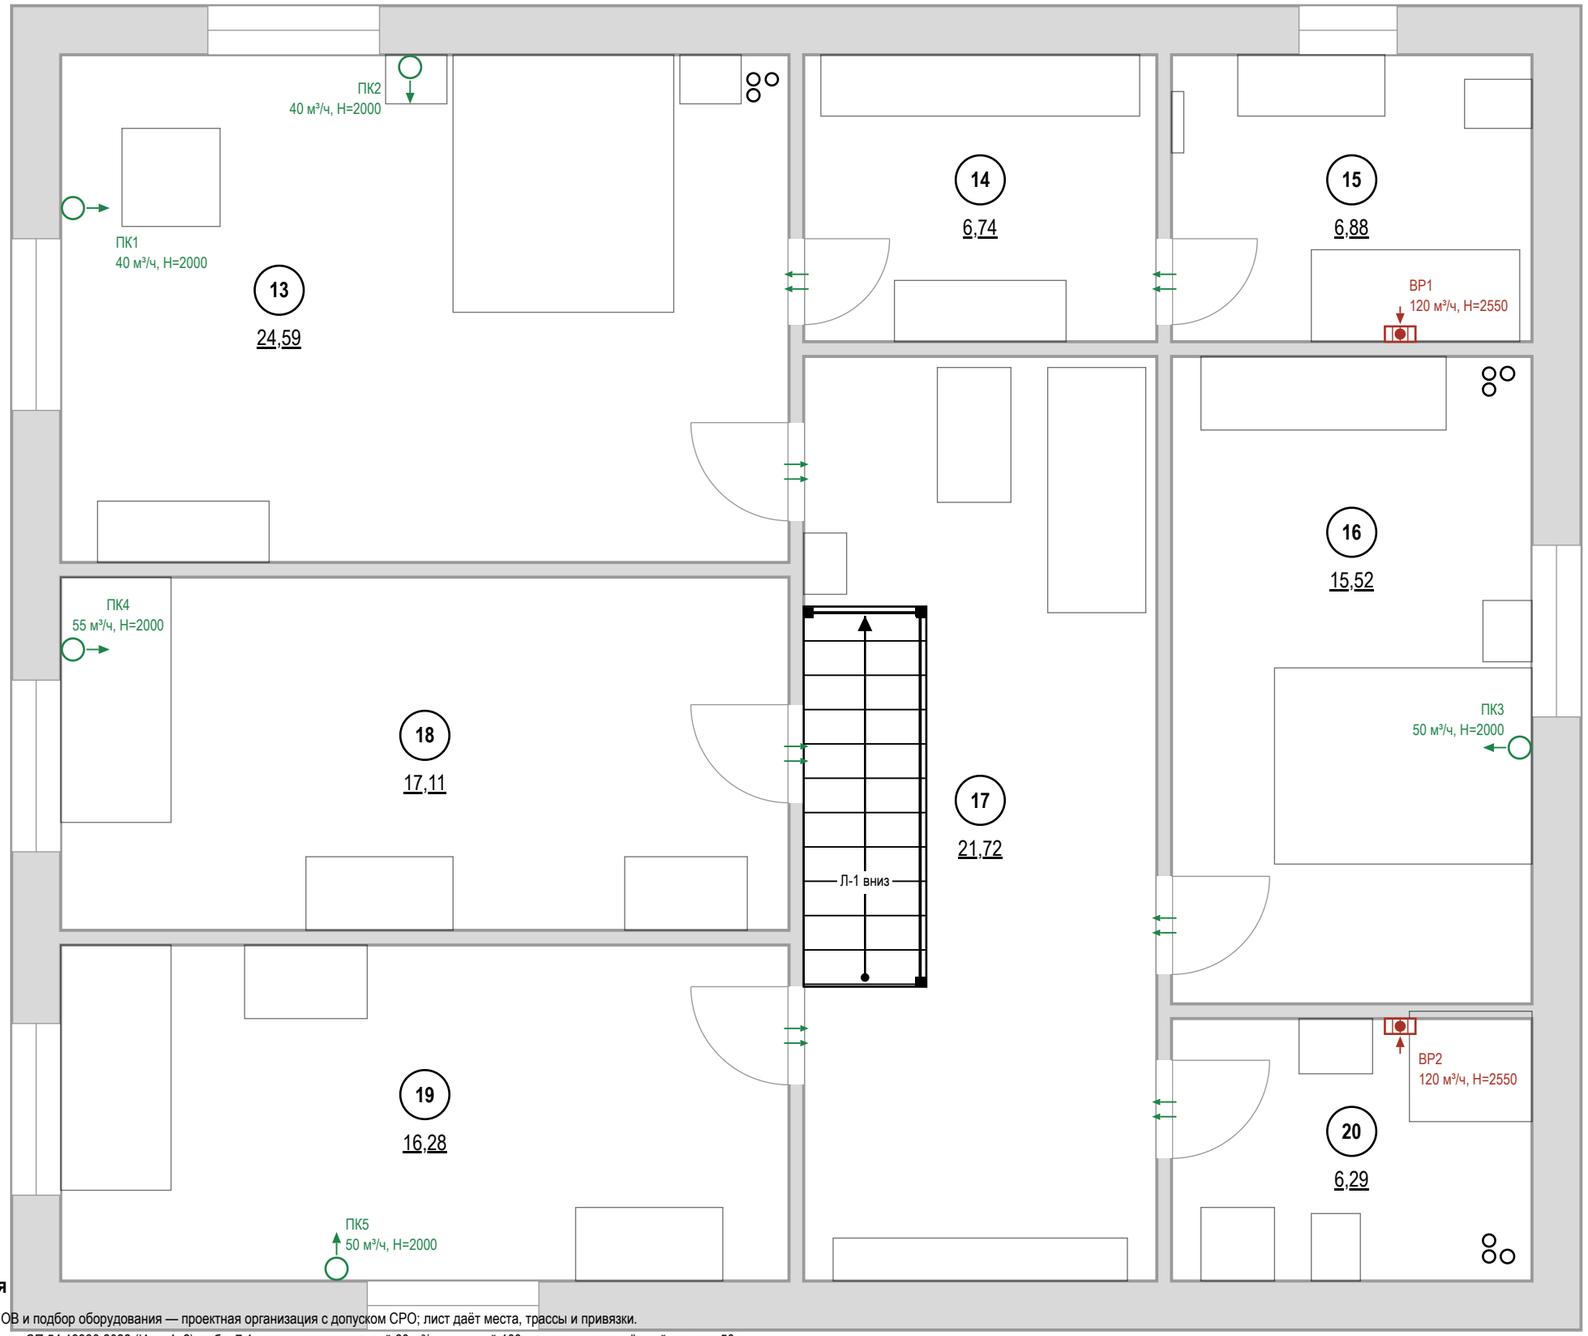

Условные обозначения

- стояк: К1 — канализация, В1 — ХВС, Т3 — ГВС
- номер помещения, площадь м²
- вытяжная решётка с бытовым вентилятором и обратным клапаном: марка, расход, Н
- приточный клапан (КИВ) в наружной стене: марка, расход, Н центра
- переток: зазор под полотном или переточная решётка

Воздухообмен, м³/ч

№	Помещение	Выт. норма	Выт. проект	Прит. норма	Прит. проект	Устройства
13	Спальня мастер			74	80	ПК1, ПК2
14	Гардеробная мастер	4				переток
15	Санузел мастер	50	120			ВР1
16	Спальня 2			47	50	ПК3
18	Спальня 3			52	55	ПК4
19	Спальня 4			49	50	ПК5
20	Санузел 2	50	120			ВР2
	Итого	**104**	**240**	**120**	**235**	


Воздухообмен квартиры — по большей из сумм притока и вытяжки: норма 120 м³/ч, проект 240 м³/ч.
Вытяжка не меньше притока — баланс сведён.

Примечания

1. Расчёт систем ОВ и подбор оборудования — проектная организация с допуском СРО; лист даёт места, трассы и привязки.
2. Нормы вытяжки — СП 54.13330.2022 (Изм. 1, 2), табл. 7.1: кухня с электроплитой 60 м³/ч, с газовой 100; ванная и совмещённый санузел 50; уборная 25; гардеробная 0,2 ч⁻¹. Приток в жилые — 3 м³/ч на 1 м² (менее 20 м² общей площади на человека), иначе 30 м³/ч на человека.
3. Вентканалы и шахты не сужать, не переносить и не закрывать; вентилятор и кухонная вытяжка — через обратный клапан, без перекрытия естественной тяги.
4. Проектные расходы — не ниже нормы, вытяжка сведена с притоком вентиляторами мокрых помещений. Клапаны — в простенке у окна, центр 2000 мм, не над кроватью, не ближе 300 мм к стоякам отопления; типоразмер — на расход.
5. Переток — зазор под полотнами межкомнатных дверей или переточная решётка.
6. Кондиционирование заданием не предусмотрено; при установке трассы фреона и дренажа (не менее 40 мм/м, в К1 через сифон) и питание заложить до черновых работ.
7. Привязки оборудования — по паспортам приобретённых моделей, до черновых работ.

					Проект: Дом 331 м²
	Лист	№ док.	Подпись	Дата	
Дизайнер	Кырлан А.С.			19.10.26	План вентиляции · Мансарда
					Стадия: П; Лист: 43; Листов: 155

выпуск 18.10.2026 № ffc1f29499 · стр. 43 из 155

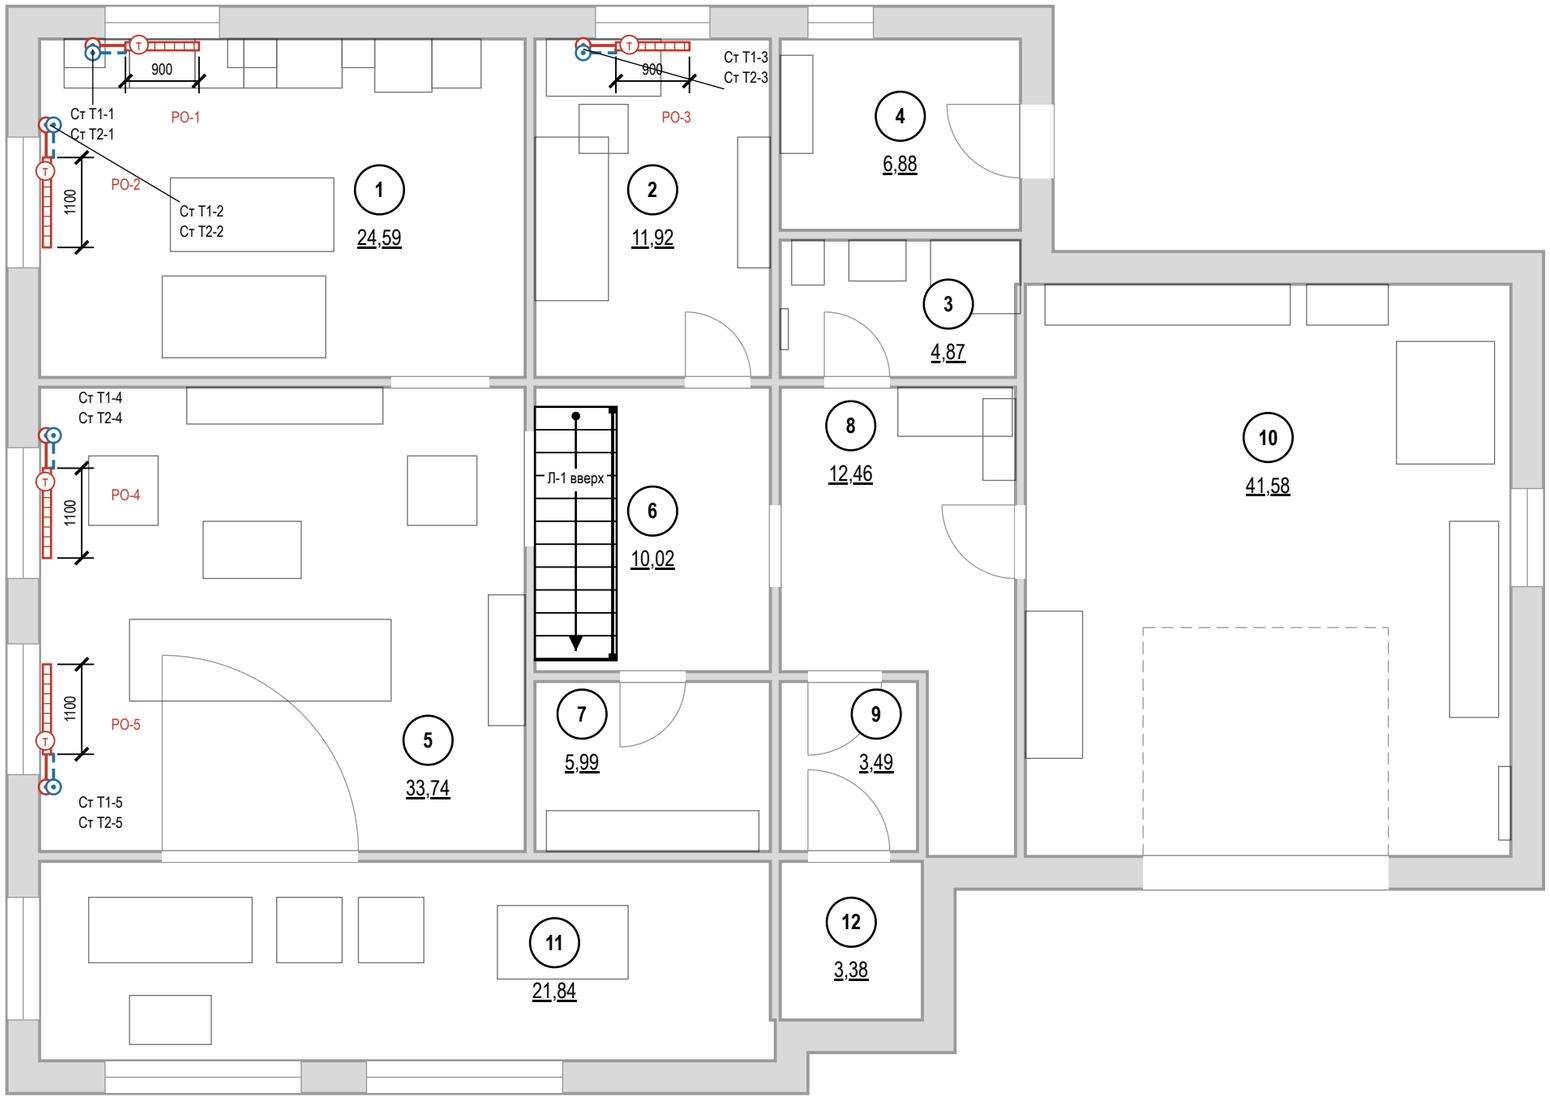

Условные обозначения

- (1) — номер помещения, площадь м²
- радиатор отопления (марка РО-N, длина по плану)
- (T) — клапан с термоголовкой на подаче
- стояк отопления, подающий (Ст T1-N)
- стояк отопления, обратный (Ст T2-N)
- T1 — отопление, подающий трубопровод
- T2 — отопление, обратный трубопровод

Ведомость радиаторов

Марка	Помещение	Тип	Д×В×Г, мм	Низ / стена	Q, Вт
РО-1	1. Кухня-столовая	панельный	900×600×100	120 / 40	расч.
РО-2	1. Кухня-столовая	панельный	1100×600×100	120 / 40	расч.
РО-3	2. Кабинет-гостевая	панельный	900×600×100	120 / 40	расч.
РО-4	5. Гостиная	панельный	1100×600×100	120 / 40	расч.
РО-5	5. Гостиная	панельный	1100×600×100	120 / 40	расч.

тип и мощность — по теплотехническому расчёту
Низ — от чистого пола, стена — зазор до задней панели, мм.

Привязки — до обмера
Стояки отопления в исходных данных не заданы: показаны у откосов окон, подводки принципиально. До черновых работ — обмер стояков и паспорта приборов; лист перевыпустить по факту.


Примечания

1. Расчёт системы отопления, теплопотерь и подбор приборов — проектная организация с допуском СРО; лист даёт места и привязки.
2. Тип, длина и мощность радиаторов — по теплотехническому расчёту; лист задаёт места, зазоры и подключение.
3. Радиаторы — под каждым окном жилых комнат и кухни, центр по оси проёма, длина 0,7 ширины окна (кратно 100); окончательно — по расчёту.
4. Зазоры радиатора: низ не менее 100 мм от чистого пола, верх не менее 100 мм до подоконника, 30–50 мм от стены до задней панели; центр по оси окна с допуском ±20 мм.
5. Радиаторы не закрывать глухими коробами и мебелью; перенос и замена приборов в многоквартирном доме — переустройство, согласование с управляющей организацией (ЖК РФ ст. 25–26); вынос на лоджию запрещён.
6. Трубы отопления через межквартирные стены не прокладывать (СП 51.13330.2011, п. 9.19); через перекрытия и перегородки — в гильзах.
7. Привязки приборов и подводок — по паспортам приобретённых радиаторов и клапанов, до черновых работ.
8. До закрытия отделкой трубопроводы отопления испытать гидростатическим давлением с оформлением акта (СП 73.13330.2016, 7.2–7.3).

					Проект: Дом 331 м²
	Лист	№ док.	Подпись	Дата	План отопления · 1-й этаж
Дизайнер	Кырлан А.С.			19.10.26	

Стадия	Лист	Листов
П	44	155

выпуск 18.10.2026 № ffc1f29499 · стр. 44 из 155

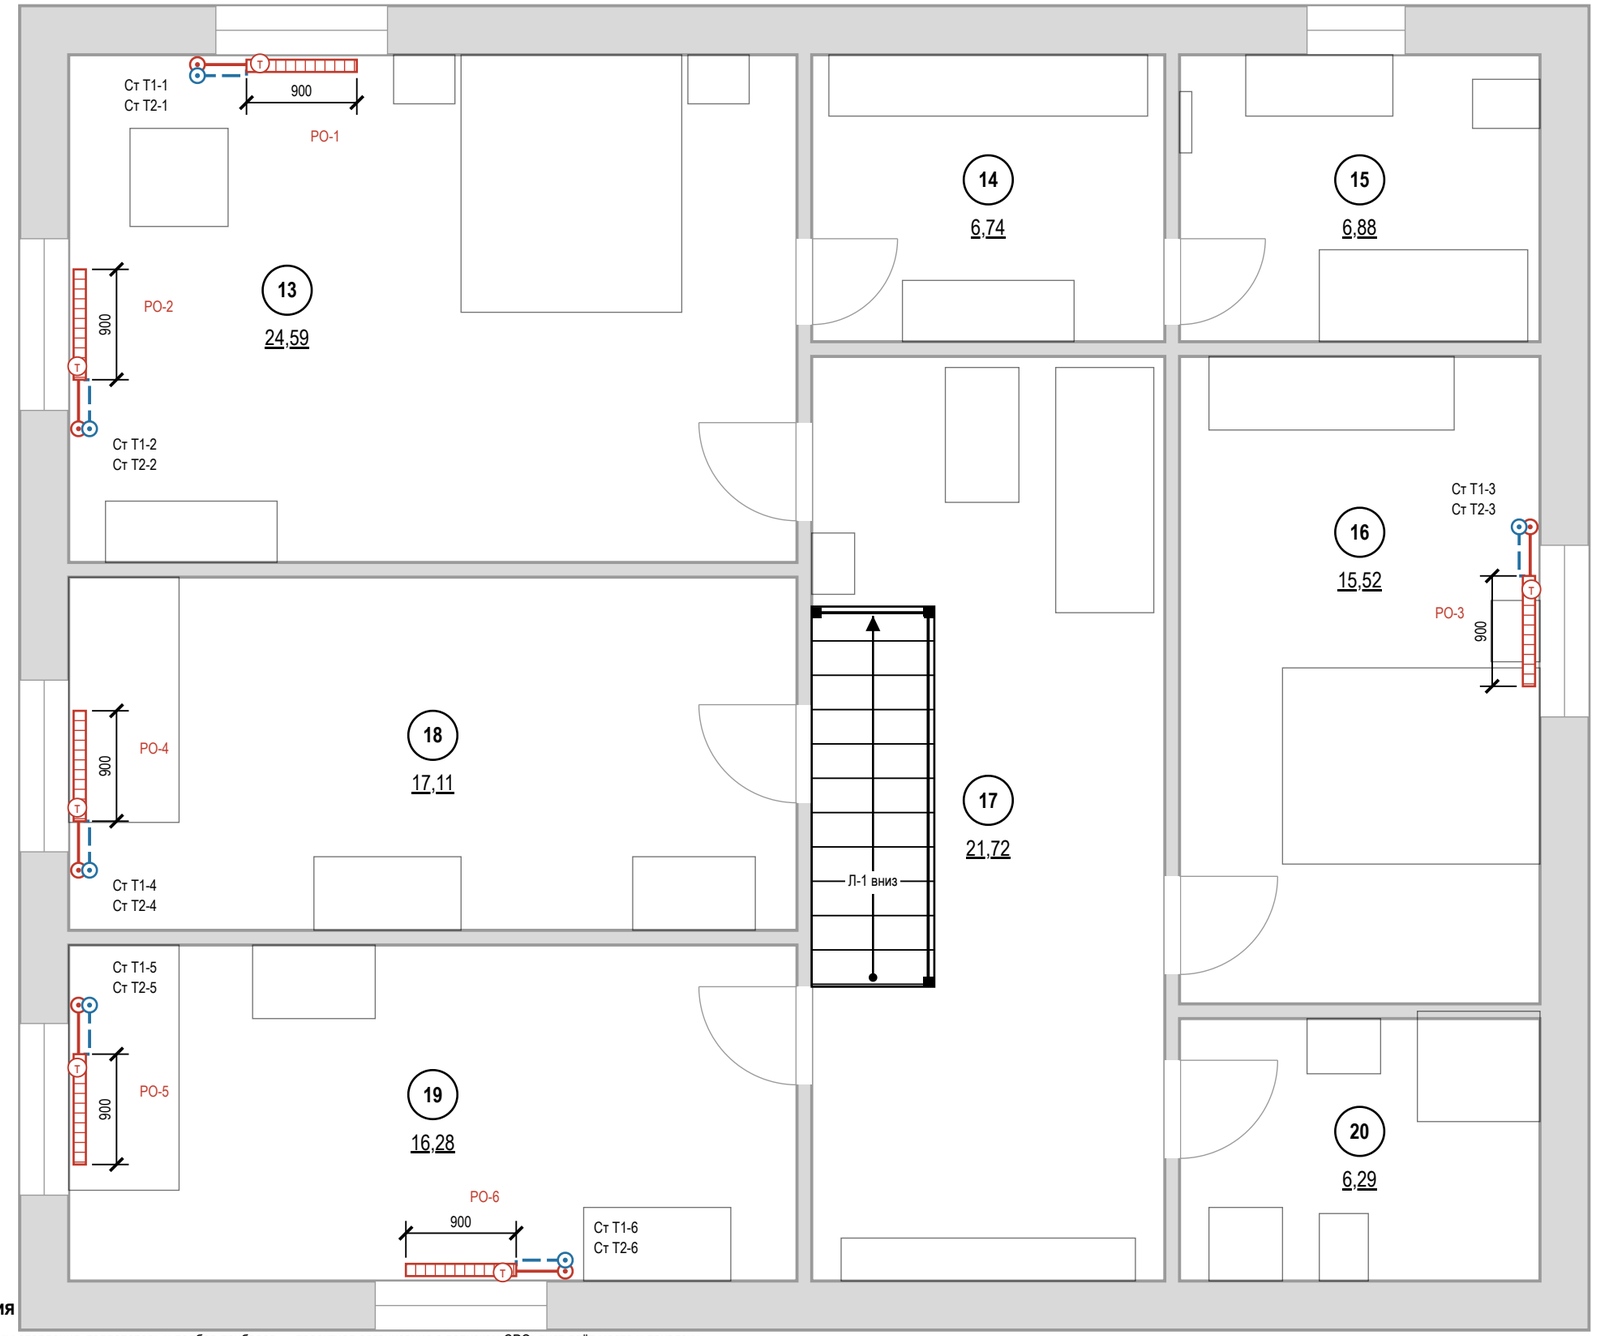

Условные обозначения

- (1) — номер помещения, площадь м²
- радиатор отопления (марка РО-N, длина по плану)
- (Т) — клапан с термоголовкой на подаче
- стояк отопления, подающий (Ст Т1-N)
- стояк отопления, обратный (Ст Т2-N)
- Т1 — отопление, подающий трубопровод
- Т2 — отопление, обратный трубопровод

Ведомость радиаторов

Марка	Помещение	Тип	Д×В×Г, мм	Низ / стена	Q, Вт
РО-1	13. Спальня мастер	панельный	900×600×100	120 / 40	расч.
РО-2	13. Спальня мастер	панельный	900×600×100	120 / 40	расч.
РО-3	16. Спальня 2	панельный	900×600×100	120 / 40	расч.
РО-4	18. Спальня 3	панельный	900×600×100	120 / 40	расч.
РО-5	19. Спальня 4	панельный	900×600×100	120 / 40	расч.
РО-6	19. Спальня 4	панельный	900×600×100	120 / 40	расч.

тип и мощность — по теплотехническому расчёту
Низ — от чистого пола, стена — зазор до задней панели, мм.

Привязки — до обмера
Стояки отопления в исходных данных не заданы: показаны у откосов окон, подводки — принципиально. До черновых работ — обмер стояков и паспорта приборов; лист перевыпустить по факту.


Примечания

1. Расчёт системы отопления, теплопотерь и подбор приборов — проектная организация с допуском СРО; лист даёт места и привязки.
2. Тип, длина и мощность радиаторов — по теплотехническому расчёту; лист задаёт места, зазоры и подключение.
3. Радиаторы — под каждым окном жилых комнат и кухни, центр по оси проёма, длина 0,7 ширины окна (кратно 100); окончательно — по расчёту.
4. Зазоры радиатора: низ не менее 100 мм от чистого пола, верх не менее 100 мм до подоконника, 30–50 мм от стены до задней панели; центр по оси окна с допуском ±20 мм.
5. Радиаторы не закрывать глухими коробами и мебелью; перенос и замена приборов в многоквартирном доме — переустройство, согласование с управляющей организацией (ЖК РФ ст. 25–26); вынос на лоджию запрещён.
6. Трубы отопления через межквартирные стены не прокладывать (СП 51.13330.2011, п. 9.19); через перекрытия и перегородки — в гильзах.
7. Привязки приборов и подводок — по паспортам приобретённых радиаторов и клапанов, до черновых работ.
8. До закрытия отделкой трубопроводы отопления испытать гидростатическим давлением с оформлением акта (СП 73.13330.2016, 7.2–7.3).








					Проект: Дом 331 м²
	Лист	№ док.	Подпись	Дата	План отопления · Мансарда
Дизайнер	Кырлан А.С.			19.10.26	Стадия: П; Лист: 45; Листов: 155

Отметки по высоте

±0,000 чистый пол пом. 1, 2, 4–10; отсчёт высот
−0,015 чистый пол пом. 3, ниже на 15 мм
−0,030 чистый пол пом. 11, 12, ниже на 30 мм
плита верх плиты разный: −0,064, −0,170 (задание на обмер)
сущ. пол снимается до плиты; не замерен (задание на обмер)

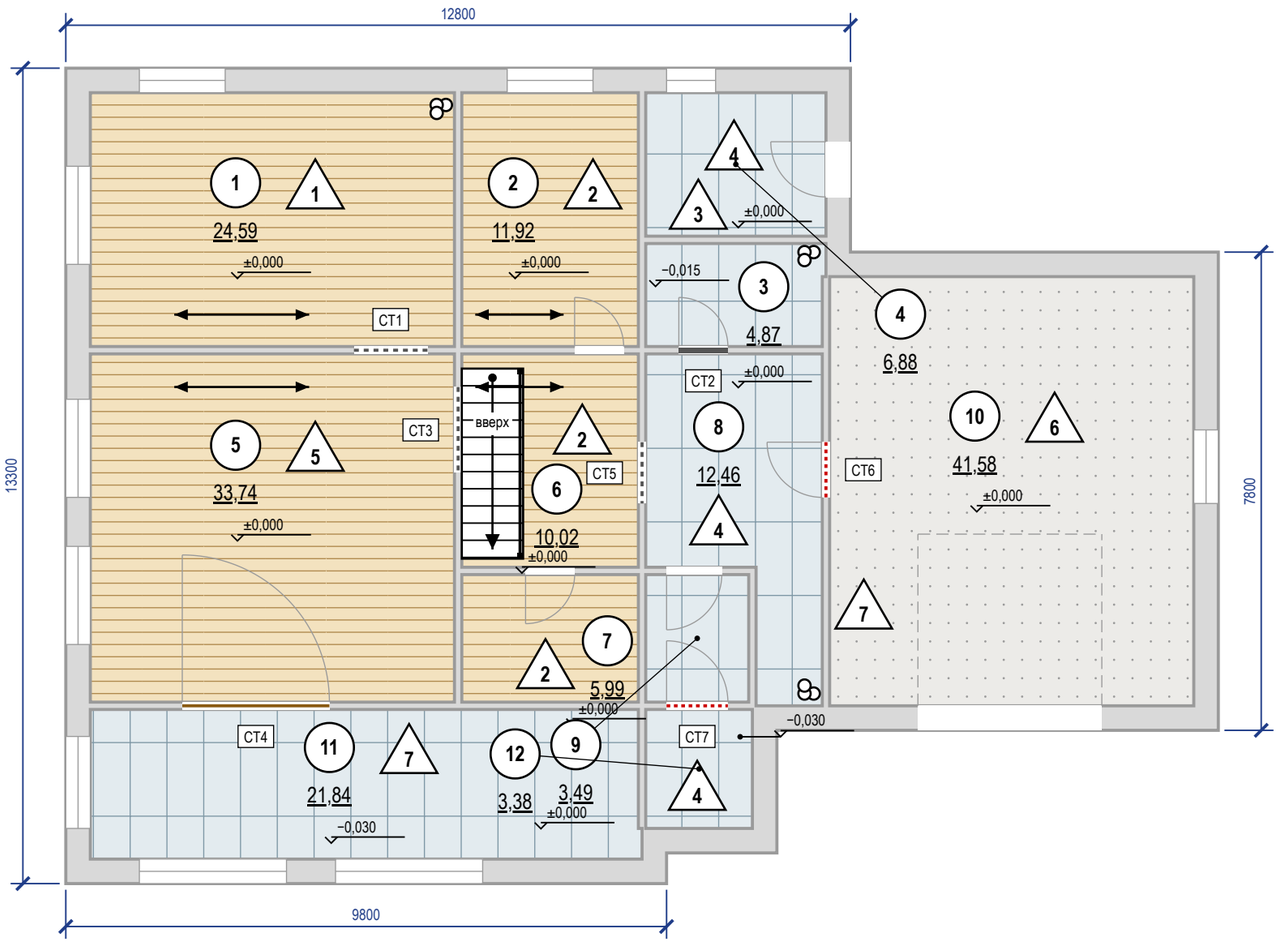

Экспликация полов

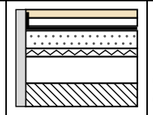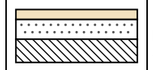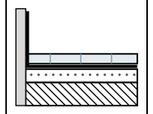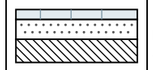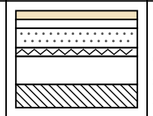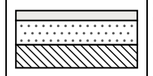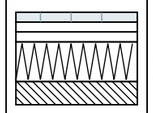
Номер помещения	Тип пола	Схема пола	Данные элементов пола (наименование, толщина, основание), мм	Площадь, м²
1	1		Инженерная доска дуб на клею — 14 Клей паркетный МС-полимерный — 1 Гидроизоляция полиуретановая, 2 слоя (зона мойки и острова) — 2 Стяжка ЦПС М300 (В22,5), фибра, по звукоизоляции — 53 Звукоизоляция — минплита 110 кг/м³ 20 Засыпка керамзитовая фр. 0–5, уплотнённая — 80 Плита перекрытия монолитная Всего 170 мм; ЧП ±0,000, верх плиты −0,170	24,59
2, 6, 7	2		Инженерная доска на клею — 14 Стяжка ЦПС М200 — 50 Плита перекрытия Всего 64 мм; ЧП ±0,000, верх плиты −0,064	27,93
3	3		Керамогранит на клею С2 TE S1 — 14 Гидроизоляция обмазочная, 2 слоя, с заведением на стены 200 мм — 2 Стяжка ЦПС М200 — 33 Плита перекрытия Всего 49 мм; ЧП −0,015, верх плиты −0,064	4,87
4, 8, 9	4		Керамогранит на клею С2 TE S1 — 14 Стяжка ЦПС М200 — 50 Плита перекрытия Всего 64 мм; ЧП ±0,000, верх плиты −0,064	22,83
5	5		Инженерная доска дуб на клею — 14 Клей паркетный МС-полимерный — 1 Стяжка ЦПС М300 (В22,5), фибра, по звукоизоляции — 55 Звукоизоляция — минплита 110 кг/м³ 20 Засыпка керамзитовая фр. 0–5, уплотнённая — 80 Плита перекрытия монолитная Всего 170 мм; ЧП ±0,000, верх плиты −0,170	33,74
10	6		Наливной полимерный пол с грунтом и кварцевой посыпкой — 3 Стяжка ЦПС М300, армированная сеткой — 61 Плита перекрытия по грунту Всего 64 мм; ЧП ±0,000, верх плиты −0,064	41,58
11, 12	7		Керамогранит 600×600×10 — 10 Клей плиточный С2 TE S1 (деформируемый) — 5 Сборное основание ГВЛВ 2×12,5 — 25 Пенополистирол экструзионный 2×50 100 Плита перекрытия монолитная Всего 140 мм; ЧП −0,030, верх плиты −0,170	25,22
			Итого	**180,76**

Примечания



1. За отметку ±0,000 принят чистый пол, не существующий (блок отметок). Площади — по чистым размерам помещений, м²; размеры — в мм.
2. Стык разнотипных покрытий — по оси дверного полотна (под полотном в закрытом положении); решение стыка — по ведомости стыков.
3. Пол санузлов ниже смежных помещений на 15 мм; гидроизоляция по стяжке с заведением на стены не менее 200 мм (СП 29.13330.2011, п. 7.2), до облицовки — тест проливом и акт скрытых работ.
4. Трубопроводы в конструкции пола не прокладываются: пирог пола 49–170 мм не вмещает выпуски канализации с уклоном — выпуски К1 ведутся по стенам над чистым полом в коробах.
5. Штучные покрытия (инженерная доска): направление — по стрелке; влажность основания по СМ не более 2,0 % (по ТУ изготовителя).
6. Ровность основания — просвет под 2-метровой рейкой не более 2 мм: пом. 1, 2, 5, 6, 7 (инженерная доска), пом. 3, 4, 8, 9 (керамогранит), пом. 10 (наливной пол); 3 мм: пом. 11, 12 (керамогранит); проверить до укладки покрытия (СП 71.13330.2017, табл. 8.5).
7. Плавающая стяжка по звукоизоляции: демпферная (кромочная) лента по контуру помещения, у стояков и колонн — до верха чистого пола (СП 51.13330.2011, п. 9.11); плинтус крепится только к стене.
8. Сетка на плитке — условная, в размер формата; точка старта и раскладка — по листу раскладки плитки.
9. Пироги полов — по экспликации полов: слои сверху вниз, толщины в мм; гидроизоляция мокрых зон — в пироге и в ведомости отделки; схема пола — без масштаба.

					Проект: Дом 331 м²
	Лист	№ док.	Подпись	Дата	План покрытий пола · 1-й этаж
Дизайнер	Кырлан А.С.			19.10.26	Стадия: П; Лист: 46; Листов: 155

выпуск 18.10.2026 № ffc1f29499 · стр. 46 из 155

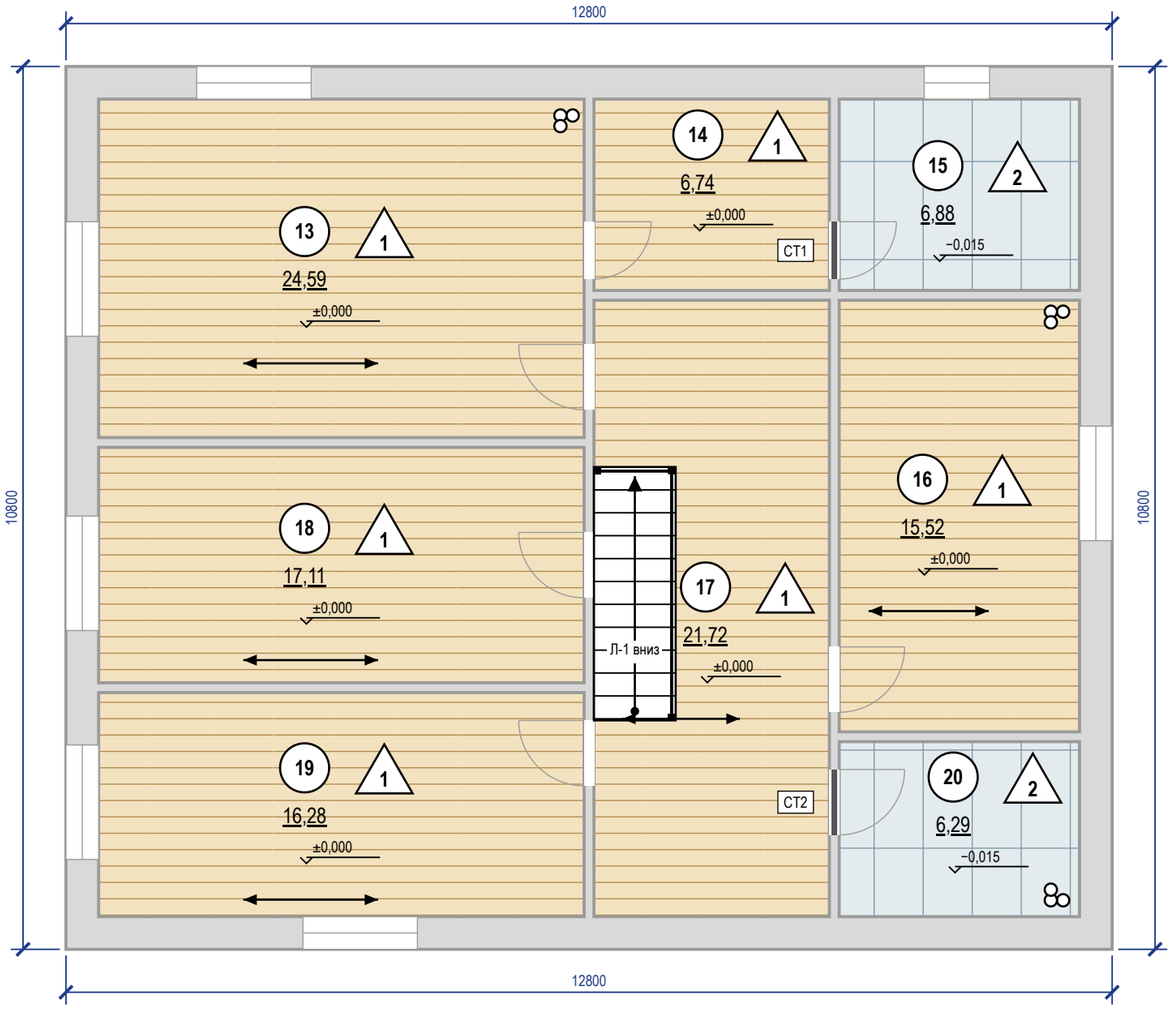

Экспликация полов

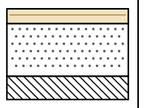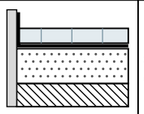Номер помещения	Тип пола	Схема пола	Данные элементов пола (наименование, толщина, основание), мм	Площадь, м²
13, 14, 16, 17, 18, 19	1		Инженерная доска на клею — 14 Стяжка ЦПС М200 — 50 Плита перекрытия Всего 64 мм; ЧП ±0,000, верх плиты −0,064	101,96
15, 20	2		Керамогранит на клею С2 TE S1 — 14 Гидроизоляция обмазочная, 2 слоя, с заведением на стены 200 мм — 2 Стяжка ЦПС М200 — 33 Плита перекрытия Всего 49 мм; ЧП −0,015, верх плиты −0,064	13,17
			Итого	**115,13**

Спецификация плинтусов

Наименование	Помещения	Длина, м (с запасом)
Плинтус МДФ под покраску 80×16, крепление к стене, окраска в цвет Farrow & Ball No. 226	13, 14, 16, 17	67
SX165, h = 69 мм, крепление к стене, окраска в цвет Farrow & Ball No. 226	18, 19	37

Отметки по высоте

±0,000 чистый пол пом. 13, 14, 16–19; отсчёт высот
−0,015 чистый пол пом. 15, 20, ниже на 15 мм
−0,064 верх плиты — расчёт, не замер (задание на обмер)
сущ. пол снимается до плиты; не замерен (задание на обмер)


Примечания

1. За отметку ±0,000 принят чистый пол, не существующий (блок отметок). Площади — по чистым размерам помещений, м²; размеры — в мм.
2. Стык разнотипных покрытий — по оси дверного полотна (под полотном в закрытом положении); решение стыка — по ведомости стыков.
3. Пол санузлов ниже смежных помещений на 15 мм за счёт меньшей толщины стяжки (верх плиты общий — по экспликации полов); гидроизоляция по стяжке с заведением на стены не менее 200 мм (СП 29.13330.2011, п. 7.2), до облицовки — тест проливом и акт скрытых работ.
4. Трубопроводы в конструкции пола не прокладываются: пирог пола 49–64 мм не вмещает выпуски канализации с уклоном — выпуски К1 ведутся по стенам над чистым полом в коробах.
5. Штучные покрытия (инженерная доска): направление — по стрелке; влажность основания по СМ не более 2,0 % (по ТУ изготовителя).
6. Ровность основания — просвет под 2-метровой рейкой не более 2 мм: пом. 13, 14, 16, 17, 18, 19 (инженерная доска), пом. 15, 20 (керамогранит); проверить до укладки покрытия (СП 71.13330.2017, табл. 8.5).
7. Сетка на плитке — условная, в размер формата; точка старта и раскладка — по листу раскладки плитки.
8. Пироги полов — по экспликации полов: слои сверху вниз, толщины в мм; гидроизоляция мокрых зон — в пироге и в ведомости отделки; схема пола — без масштаба.


					Проект: Дом 331 м²
	Лист	№ док.	Подпись	Дата	План покрытий пола · Мансарда
Дизайнер	Кырлан А.С.			19.10.26	Стадия: П; Лист: 47; Листов: 155

выпуск 18.10.2026 № ffc1f29499 · стр. 47 из 155


Фрагмент 1. Санузел 1 этажа (пом. 3). Пол 600×600, шов 2 мм, М 1:40

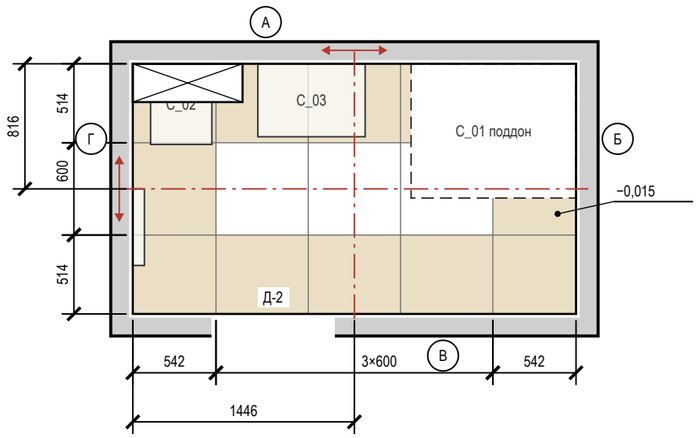

Фрагмент 2. Санузел мастер (пом. 15). Пол 600×600, шов 2 мм, М 1:40

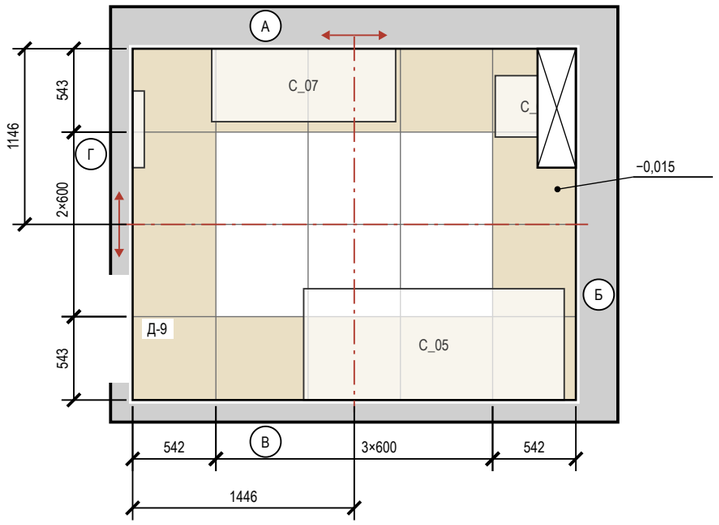

Фрагмент 3. Санузел 2 (пом. 20). Пол 600×600, шов 2 мм, М 1:40

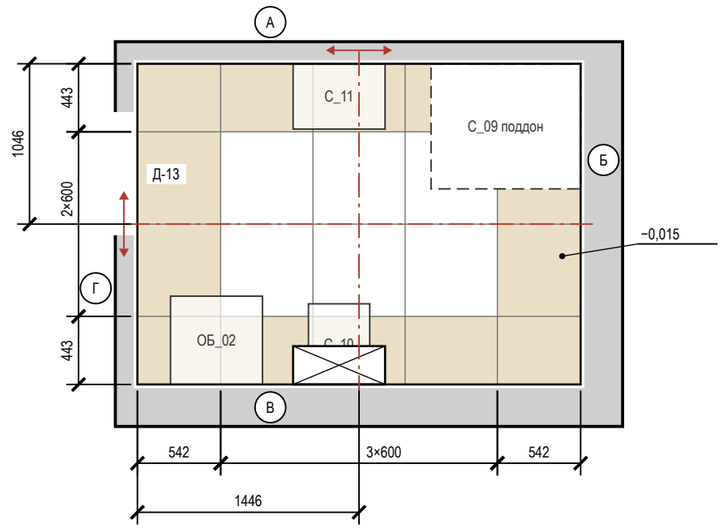

Ведомость плитки

Помещение, поверхность	Плитка, код	Формат	Шов	S, м²	Целых	Подр.	С запасом
Санузел 1 этажа, пол	аналог: керамогранит под травертин	600×600	2	4,87	2	12	16
Санузел 1 этажа, стены А–Г	аналог: керамогранит под травертин	600×1200	2	19,67	11	19	34
Санузел 1 этажа, короб инсталляции	аналог: керамогранит под травертин	600×1200	2	1,64	0	6	7
Санузел мастер, пол	аналог: керамогранит под травертин	600×600	2	6,88	6	14	22
Санузел мастер, стены А–Г	аналог: керамогранит под травертин	600×1200	2	19,01	14	21	39
Санузел мастер, короб инсталляции	аналог: керамогранит под травертин	600×1200	2	1,73	0	6	7
Санузел 2, пол	аналог: керамогранит под травертин	600×600	2	6,29	5	14	21
Санузел 2, стены А–Г	аналог: керамогранит под травертин	600×1200	2	17,04	14	21	39
Санузел 2, короб инсталляции	аналог: керамогранит под травертин	600×1200	2	1,47	1	3	5
Котельная, пол	A8UZ	600×1200	2	6,88	0	10	11
Прихожая, пол	A8UZ	600×1200	2	12,46	3	12	17
Тамбур, пол	A8UZ	600×1200	2	3,49	0	6	7
Веранда, пол	A8UZ	600×1200	2	21,84	13	32	50
Крыльцо, пол	A8UZ	600×1200	2	3,38	0	6	7
Итого 600×600				18,04	13	40	59
Итого 600×1200				**108,60**	**56**	**142**	**223**

Ведомость материалов

Материал	Класс, код	Норма расхода	Кол-во
Затирка	CG2WA Mapei Ultracolor Plus 132	(a+b)/ab·шов·t·1,6	6,9 кг
Затирка	CG2WA	(a+b)/ab·шов·t·1,6	3,8 кг
Клей	C2 TE S1 Ceresit CM 17	1,5 кг/м²·мм, слой 5	682 кг (28 меш.)
Клей	C2 TE S1	1,5 кг/м²·мм, слой 5	370 кг (15 меш.)
Гидроизоляция	обмазочная, 2 слоя: пол, стены по периметру и зоны замачивания	по ТУ	43,1 м²
Демпф. лента	по периметру пола из плитки		85,5 м

Условные обозначения

- плитка целая; тонкая линия — шов
- плитка с подрезкой (размер — на цепочке)
- ось старта; стрелки — направление укладки
- сантехприбор: габарит, высота по практике
- поддон душа — плитку пола под ним не кладут
- короб инсталляции: плитка пола — до короба
- отметка чистого пола на полке выноски, м
- (А) обозначение стены А–Г (как на развёртках)


Примечания

1. Раскладка от чистовых размеров: стены санузлов теряют 10 + 5 + 9 = 24 мм на сторону (штукатурка, клей, плитка); подрезки — чистые, без шва.
2. Старт — от центра помещения (штрихпунктир, стрелки — направление укладки); размер старта — от чистовых стен Г и А.
3. Раскладка пола «Котельная» и пола «Прихожая» и пола «Тамбур» и пола «Веранда» и пола «Крыльцо» — на листе «Раскладка плитки. Котельная. Прихожая. Тамбур. Веранда. Крыльцо».
4. Калибр партии не задан — до укладки замерить (рабочий размер W, ГОСТ 13996-2019) и пересчитать подрезки.
5. Количество: целые по раскладке + по одной на подрезку, запас 10 %; один артикул — одна партия и тон. Исключены поддон, короб, проёмы и места за коробом; S — по чистым граням: стены нетто = зона облицовки по ведомости отделки − место за коробом инсталляции 2,51 м² (плитку за коробом не кладут), короб — отдельной строкой.
6. Клей C2 TE S1 Ceresit CM 17; C2 TE S1 (ГОСТ Р 56387-2018), затирка CG2WA Mapei Ultracolor Plus 132; CG2WA; расход — по ТУ выбранной марки.
7. Гидроизоляция: пол и стены 200 мм от ЧП; у душа — до 2000 и 500 мм за поддон, над ванной — до 2000 и 300 мм за борт (см. развёртки); акт скрытых работ, пролив 24 ч.
8. Швы пола совмещены со швами стены А; по периметру — демпферная лента.
9. Отметка чистого пола −0,015, порог 15 мм; стык с соседним покрытием — по оси полотна двери.


					Проект: Дом 331 м²
	Лист	№ док.	Подпись	Дата	
Дизайнер	Кырлан А.С.			19.10.26	Раскладка плитки. Планы полов

Стадия	Лист	Листов
П	48	155


Фрагмент 1. Котельная (пом. 4). Пол 600×1200, шов 2 мм, М 1:50

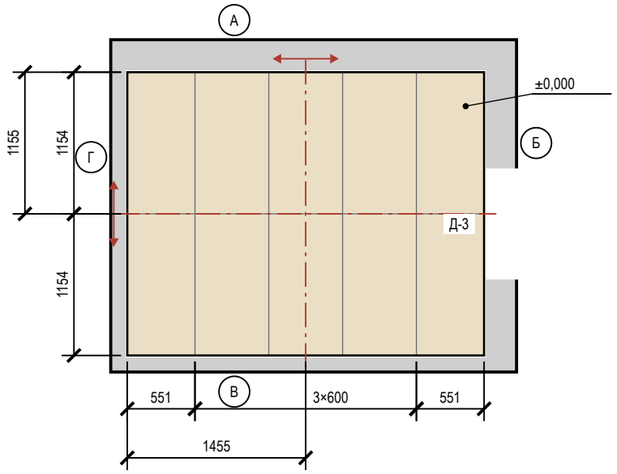

Фрагмент 2. Прихожая (пом. 8). Пол 600×1200, шов 2 мм, М 1:50

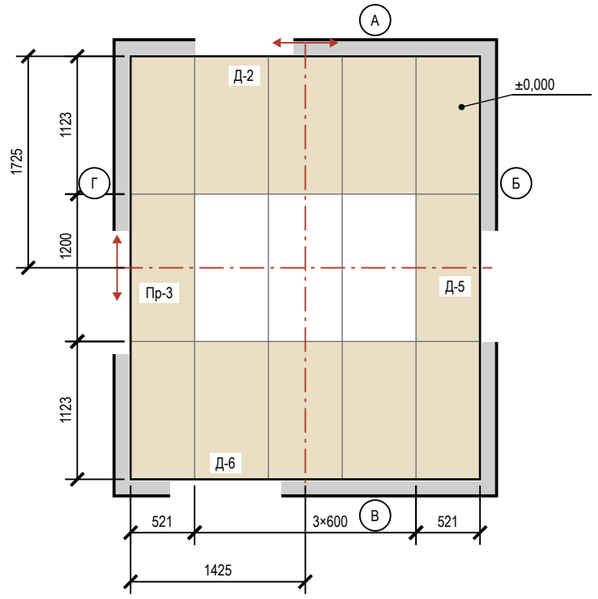


Фрагмент 3. Тамбур (пом. 9). Пол 600×1200, шов 2 мм, М 1:50

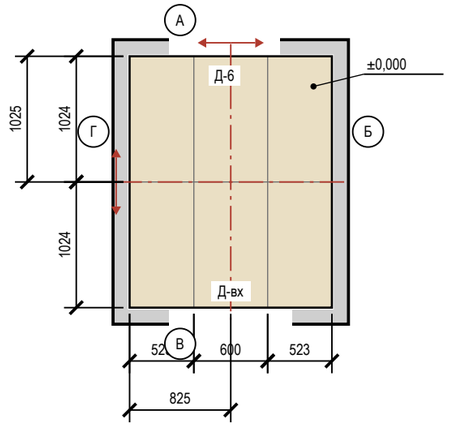

Условные обозначения

- плитка целая; тонкая линия — шов
- плитка с подрезкой (размер — на цепочке)
- ось старта; стрелки — направление укладки
- отметка чистого пола на полке выноски, м
- А — обозначение стены А–Г (как на развёртках)

Фрагмент 4. Веранда (пом. 11). Пол 600×1200, шов 2 мм, М 1:50

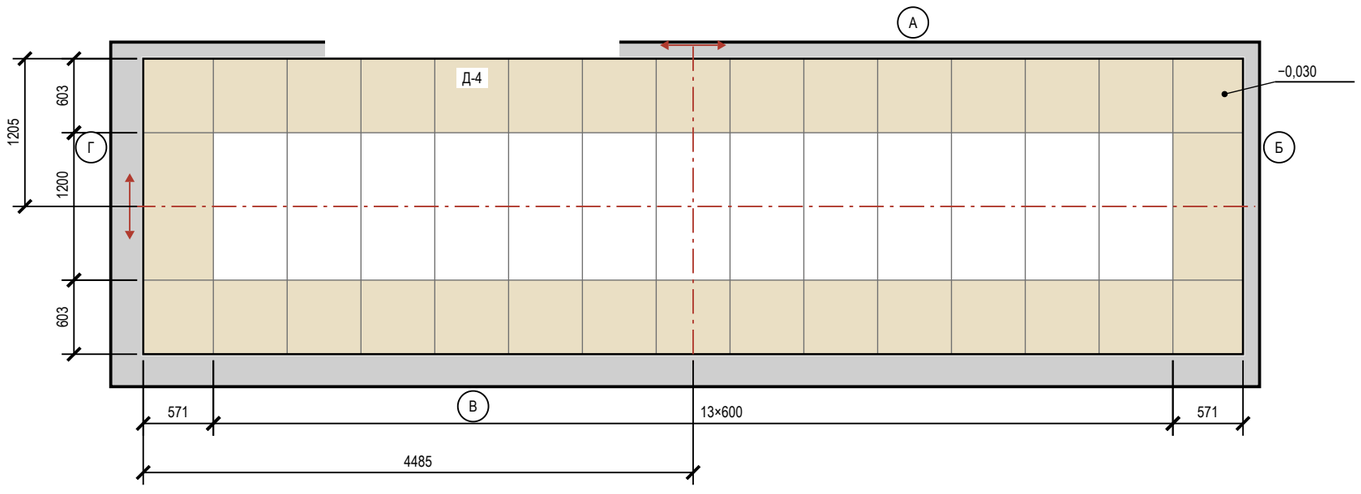

Подсчёт плитки

Поверхность	Формат	S, м²	Целых	Подр.	С запасом
Котельная, пол	600×1200	6,88	0	10	11
Прихожая, пол	600×1200	12,46	3	12	17
Тамбур, пол	600×1200	3,49	0	6	7
Веранда, пол	600×1200	21,84	13	32	50

Примечания

1. Котельная: керамогранит 600×1200, длинная сторона — вдоль стен Б и Г, шов 2 мм, прямая раскладка от центра. Стены окрашены: раскладка от чистового контура минус штукатурка и шпаклёвка 15 мм на сторону (принято); подрезки 551 / 1154 мм, срез — под плинтус.
2. Котельная: деформационный зазор по периметру 8–10 мм под плинтусом; в проёмах — стык с соседним покрытием по оси полотна двери. Клей C2 TE S1, затирка CG2WA.
3. Прихожая: керамогранит 600×1200, длинная сторона — вдоль стен Б и Г, шов 2 мм, прямая раскладка от центра. Стены окрашены: раскладка от чистового контура минус штукатурка и шпаклёвка 15 мм на сторону (принято); подрезки 521 / 1123 мм, срез — под плинтус.
4. Прихожая: деформационный зазор по периметру 8–10 мм под плинтусом; в проёмах — стык с соседним покрытием по оси полотна двери. Клей C2 TE S1, затирка CG2WA.
5. Тамбур: керамогранит 600×1200, длинная сторона — вдоль стен Б и Г, шов 2 мм, прямая раскладка от центра. Стены окрашены: раскладка от чистового контура минус штукатурка и шпаклёвка 15 мм на сторону (принято); подрезки 523 / 1024 мм, срез — под плинтус.
6. Тамбур: деформационный зазор по периметру 8–10 мм под плинтусом; в проёмах — стык с соседним покрытием по оси полотна двери. Клей C2 TE S1, затирка CG2WA.
7. Веранда: керамогранит 600×1200, длинная сторона — вдоль стен Б и Г, шов 2 мм, прямая раскладка от центра. Стены окрашены: раскладка от чистового контура минус штукатурка и шпаклёвка 15 мм на сторону (принято); подрезки 571 / 603 мм, срез — под плинтус.
8. Веранда: деформационный зазор по периметру 8–10 мм под плинтусом; в проёмах — стык с соседним покрытием по оси полотна двери. Клей C2 TE S1, затирка CG2WA.
9. Клей, затирка и итог по форматам — в ведомостях листа «Раскладка плитки. Планы полов».

					Проект: Дом 331 м²
	Лист	№ док.	Подпись	Дата	Раскладка плитки. Котельная. Прихожая. Тамбур. Веранда
Дизайнер	Кырлан А.С.			19.10.26	

Стадия	Лист	Листов
П	49	155

выпуск 18.10.2026 № ffc1f29499 · стр. 49 из 155



					Проект: Дом 331 м²
	Лист	№ док.	Подпись	Дата	
Дизайнер	Кырлан А.С.			19.10.26	Визуализация. Вид сверху

Стадия	Лист	Листов
П	50	155

выпуск 18.10.2026 № ffc1f29499 · стр. 50 из 155



					Проект: Дом 331 м²			
	Лист	№ док.	Подпись	Дата				
Дизайнер	Кырлан А.С.			19.10.26	Визуализация. Вид сверху	Стадия	Лист	Листов
						П	51	155

выпуск 18.10.2026 № ffc1f29499 · стр. 51 из 155



					Проект: Дом 331 м²
	Лист	№ док.	Подпись	Дата	
Дизайнер	Кырлан А.С.			19.10.26	Визуализация: Кухня-столовая

Стадия	Лист	Листов
П	52	155

выпуск 18.10.2026 № ffc1f29499 · стр. 52 из 155



					Проект: Дом 331 м²	
	Лист	№ док.	Подпись	Дата	Визуализация: Кухня-столовая	Стадия / Лист / Листов
Дизайнер	Кырлан А.С.			19.10.26		П / 53 / 155

выпуск 18.10.2026 № ffc1f29499 · стр. 53 из 155

Развёртка стены А


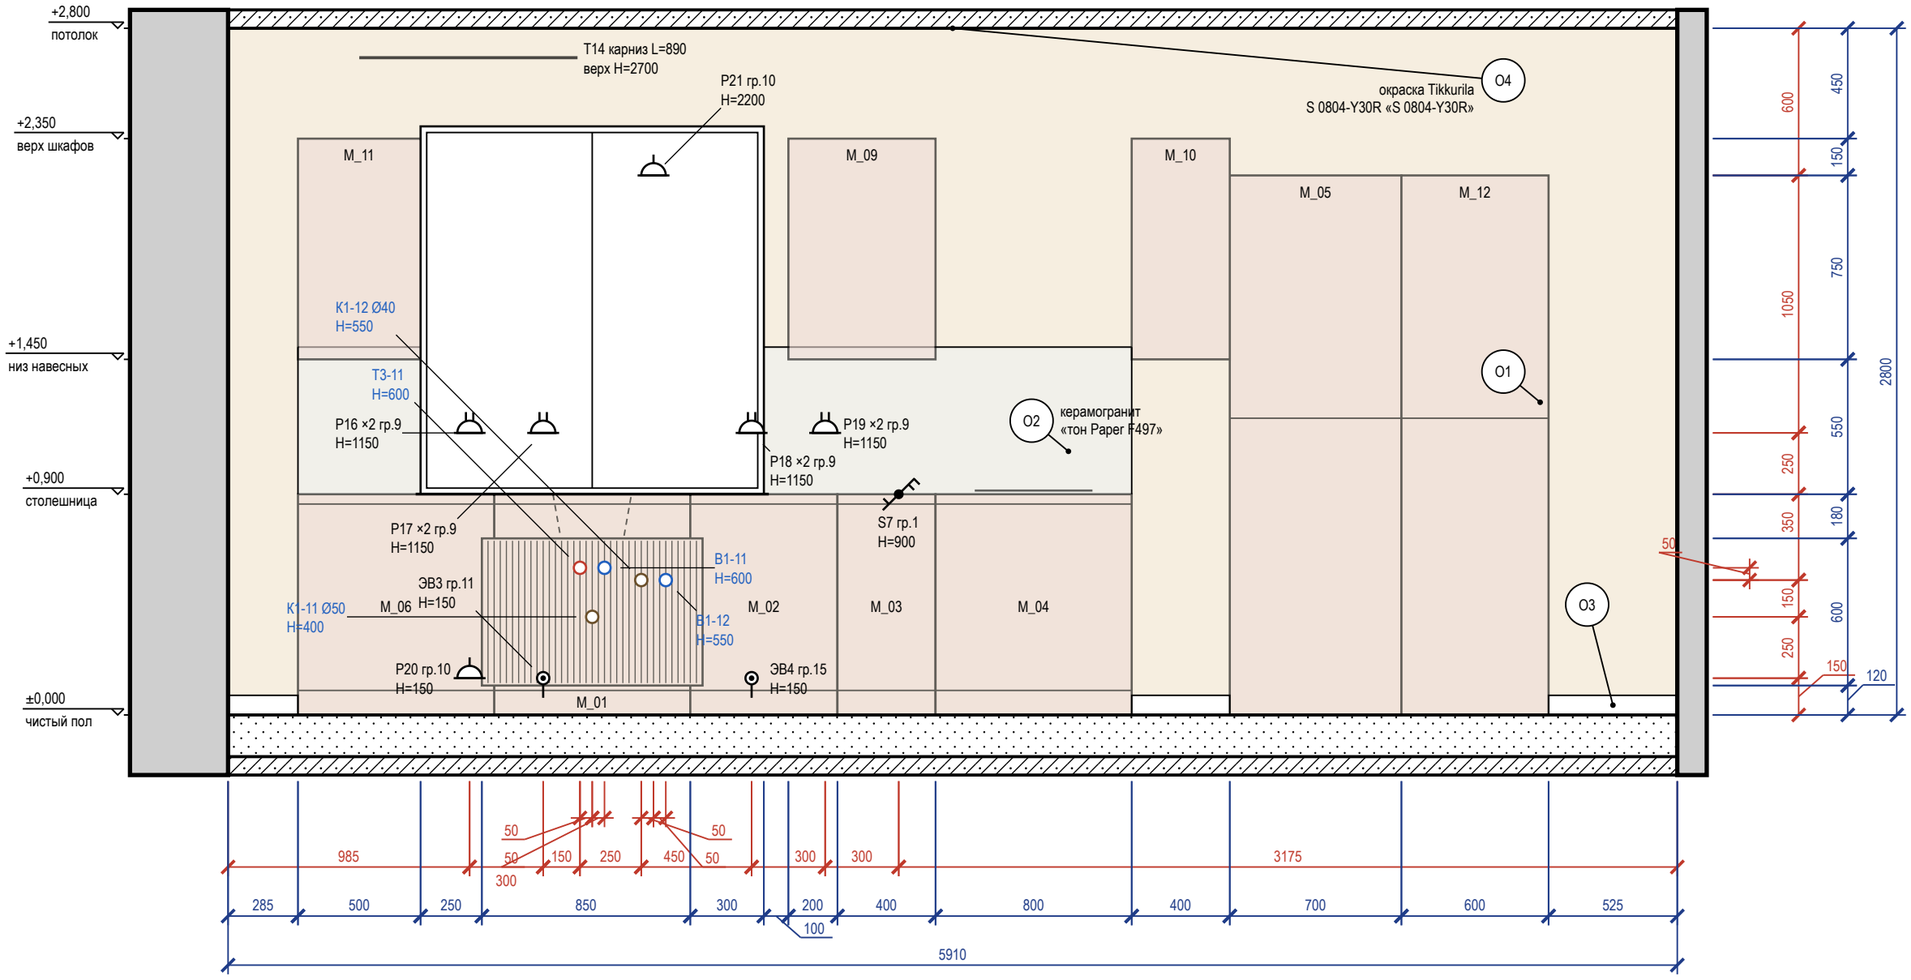


Схема развёрток (М 1:100)

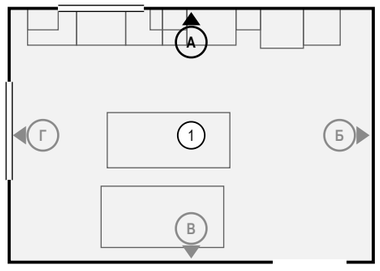

Ведомость отделки (на листе)

Марка	Поверхность	Материал, изделие	Цвет, код	Кол.
O1	стены	окраска, Tikkurila Luja 7, шелковисто-матовая, подготовка К3	NCS S 0804-Y30R «S 0804-Y30R»	12,4 м²
O2	фартук	керамогранит, аналог: керамогранит матовый, тон F497, затирка CG2WA	#F1F1EC «тон Paper F497»	1,2 м²
O3	плинтус	плинтус МДФ, h 80 мм, аналог: плинтус МДФ под окраску 80×16 мм, полуглянцевая	NCS S 0804-Y30R «S 0804-Y30R»	1,2 м
O4	потолок	окраска, Tikkurila Luja 7, матовая, подготовка Q3	NCS S 0804-Y30R «S 0804-Y30R»	24,6 м²

Визуализация этой стены — лист 52



Примечания

1. Размеры — в мм от чистовых поверхностей стен; условные обозначения и общие указания — лист 2.
2. Выводы ВК — коды и высоты по листу выводов сантехники.
3. Карнизы (шины) — по ведомости текстиля декоратора; длина L и верх H — по развёртке, крепление — до окраски потолка.
4. Выводы кухонной техники — по утверждённому проекту кухни: привязки выводов даются от осей модулей гарнитура.

					Проект: Дом 331 м²
	Лист	№ док.	Подпись	Дата	Развёртка стены А. Кухня-столовая (пом. 1), кухонный фронт
Дизайнер	Кырлан А.С.			19.10.26	

Стадия	Лист	Листов
П	54	155

выпуск 18.10.2026 № ffc1f29499 · стр. 54 из 155

Развёртка стены Б


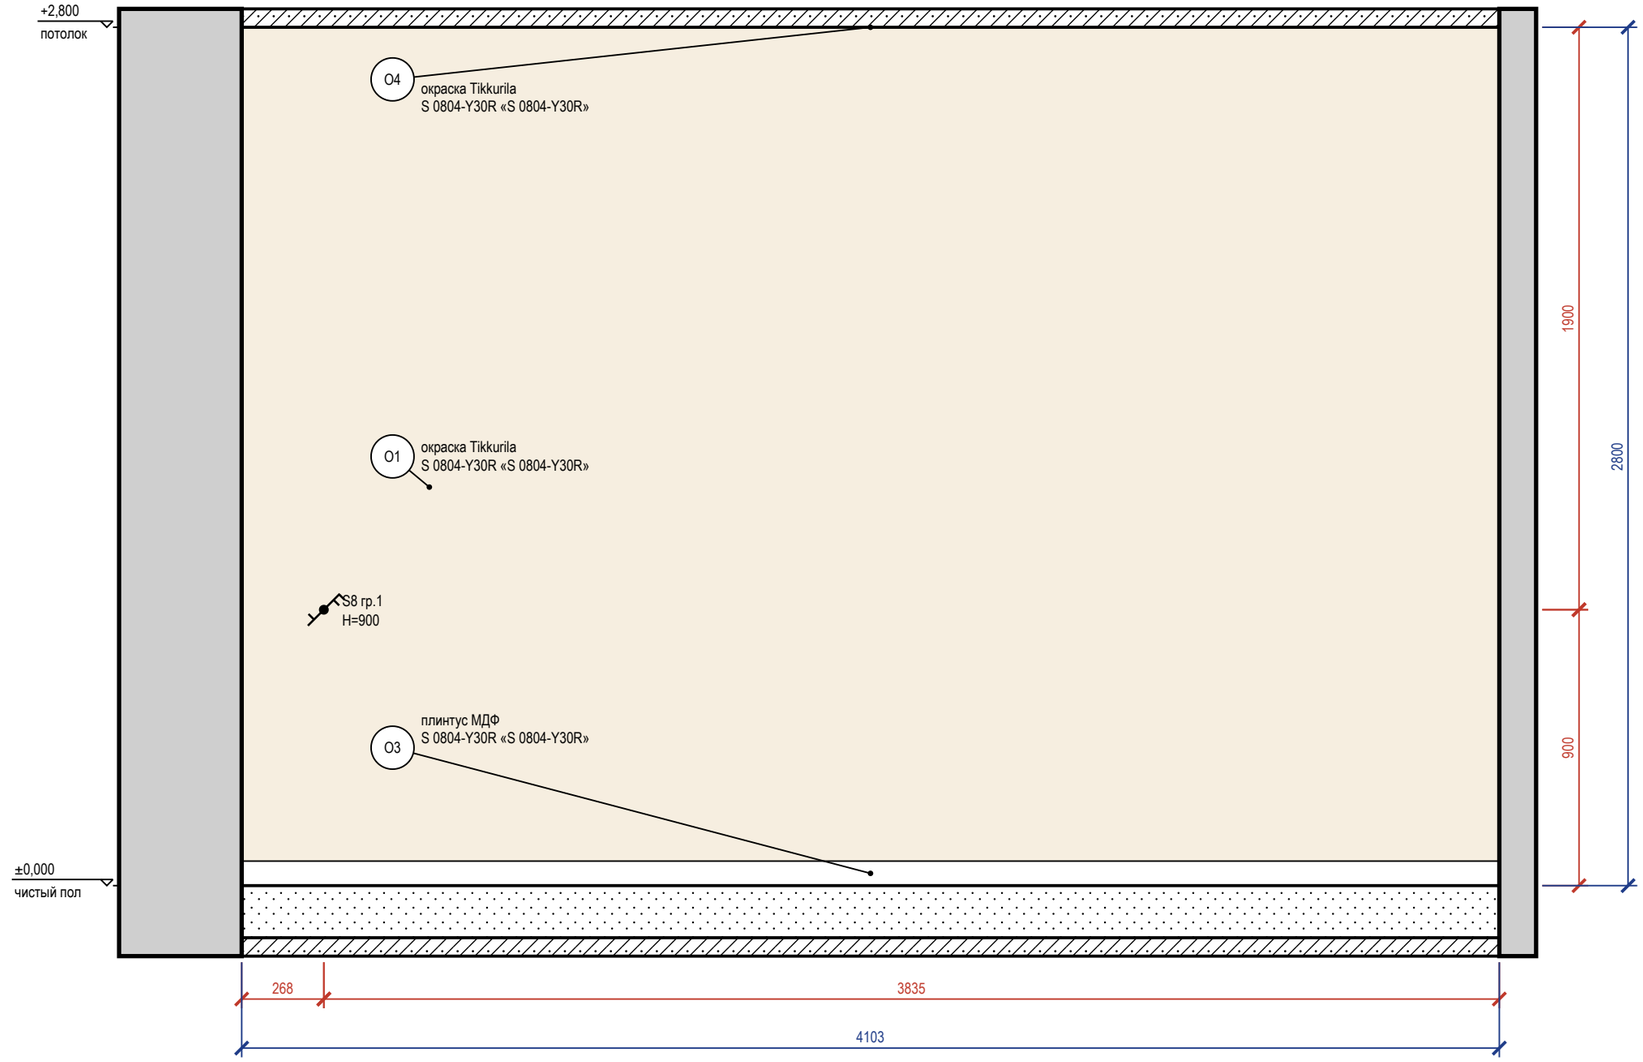


Схема развёрток (М 1:100)

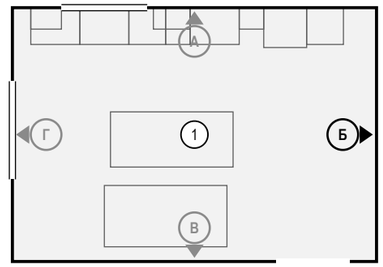

Ведомость отделки (на листе)

Марка	Поверхность	Материал, изделие	Цвет, код	Кол.
О1	стены	окраска, Tikkurila Luja 7, шелковисто-матовая, подготовка К3	NCS S 0804-Y30R «S 0804-Y30R»	11,5 м²
О3	плинтус	плинтус МДФ, h 80 мм, аналог: плинтус МДФ под окраску 80×16 мм, полуглянцевая	NCS S 0804-Y30R «S 0804-Y30R»	4,1 м
О4	потолок	окраска, Tikkurila Luja 7, матовая, подготовка Q3	NCS S 0804-Y30R «S 0804-Y30R»	24,6 м²

Примечания

1. Размеры — в мм от чистовых поверхностей стен; условные обозначения и общие указания — лист 2.

					Проект: Дом 331 м²
	Лист	№ док.	Подпись	Дата	Развёртка стены Б. Кухня-столовая (пом. 1)
Дизайнер	Кырлан А.С.			19.10.26	

Стадия	Лист	Листов
П	55	155

выпуск 18.10.2026 № ffc1f29499 · стр. 55 из 155

Развёртка стены В


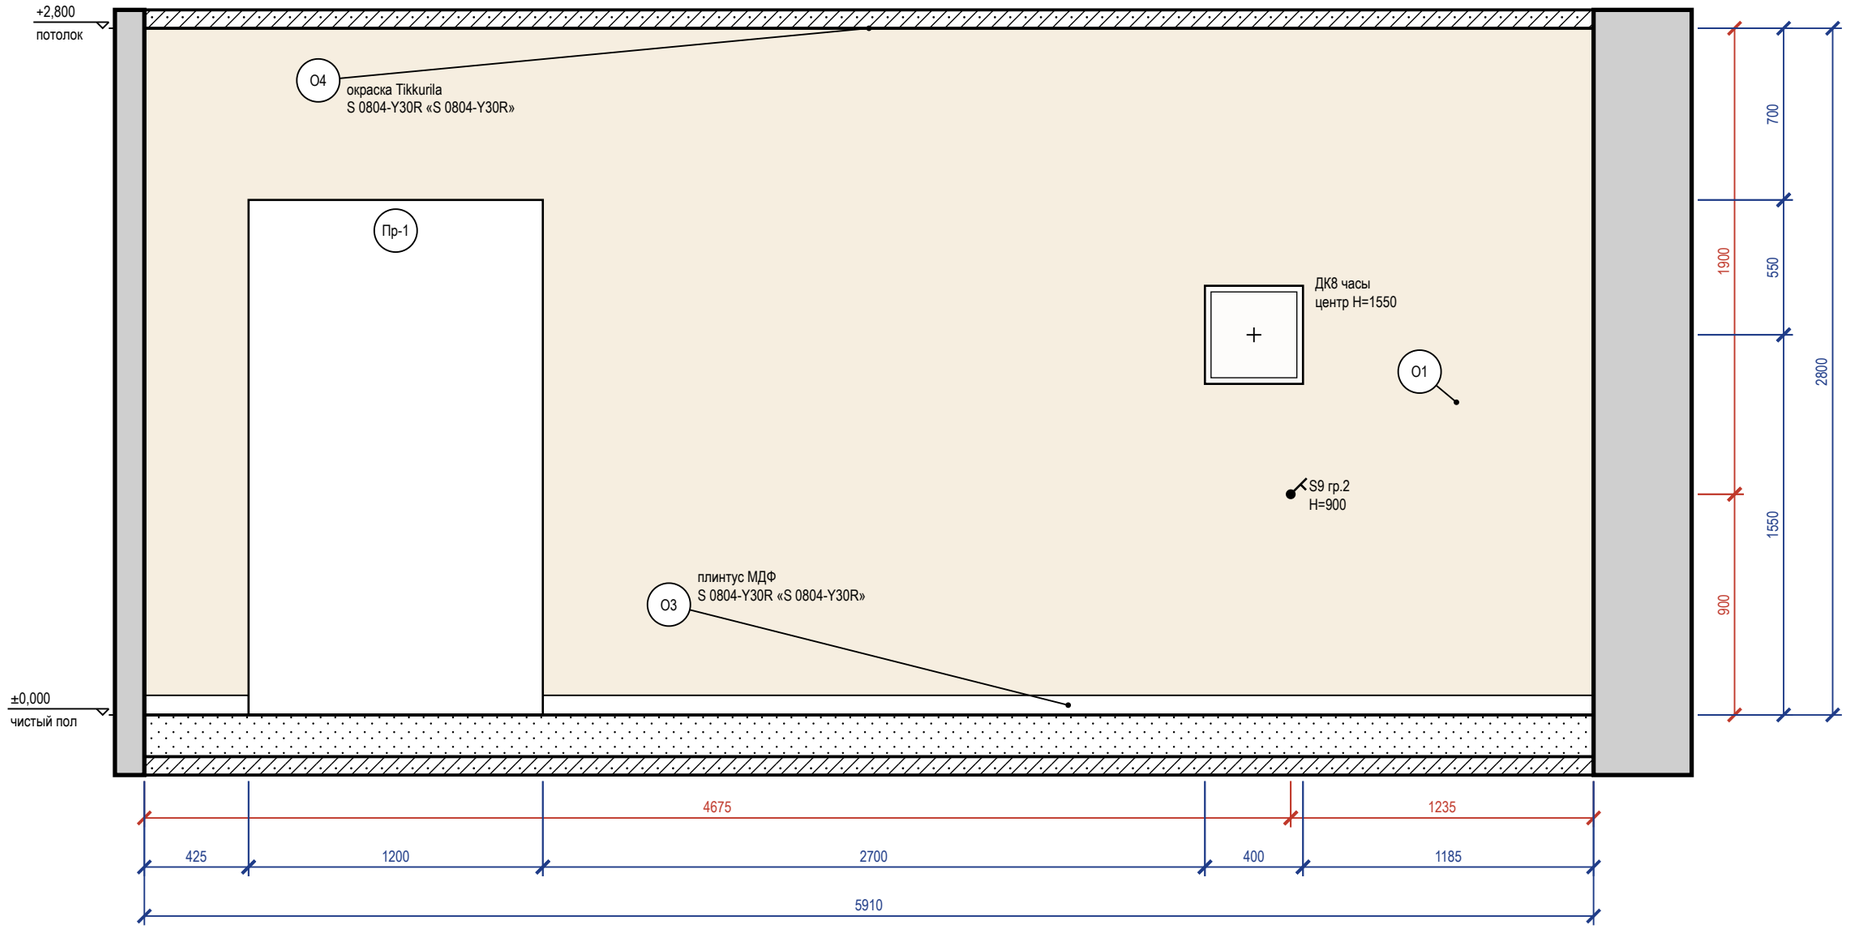



Схема развёрток (М 1:100)

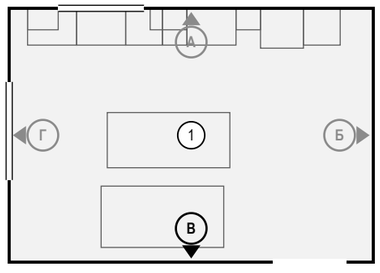

Ведомость отделки (на листе)

Марка	Поверхность	Материал, изделие	Цвет, код	Кол.
О1	стены	окраска, Tikkurila Luja 7, шелковисто-матовая, подготовка К3	NCS S 0804-Y30R «S 0804-Y30R»	14 м²
О3	плинтус	плинтус МДФ, h 80 мм, аналог: плинтус МДФ под окраску 80×16 мм, полуглянцевая	NCS S 0804-Y30R «S 0804-Y30R»	4,7 м
О4	потолок	окраска, Tikkurila Luja 7, матовая, подготовка Q3	NCS S 0804-Y30R «S 0804-Y30R»	24,6 м²

Визуализация этой стены

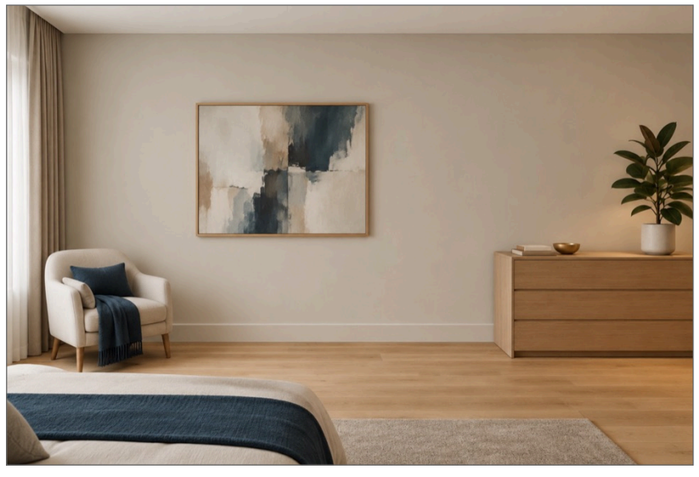

Примечания

1. Размеры — в мм от чистовых поверхностей стен; условные обозначения и общие указания — лист 2.
2. Картины и зеркала крепить к основанию по паспорту изделия (закладные и анкеры — в перечне скрытых работ); крест — ось центра предмета.

					Проект: Дом 331 м²
	Лист	№ док.	Подпись	Дата	Развёртка стены В. Кухня-столовая (пом. 1)
Дизайнер	Кырлан А.С.			19.10.26	

Стадия	Лист	Листов
П	56	155

выпуск 18.10.2026 № ffc1f29499 · стр. 56 из 155

Развёртка стены Г


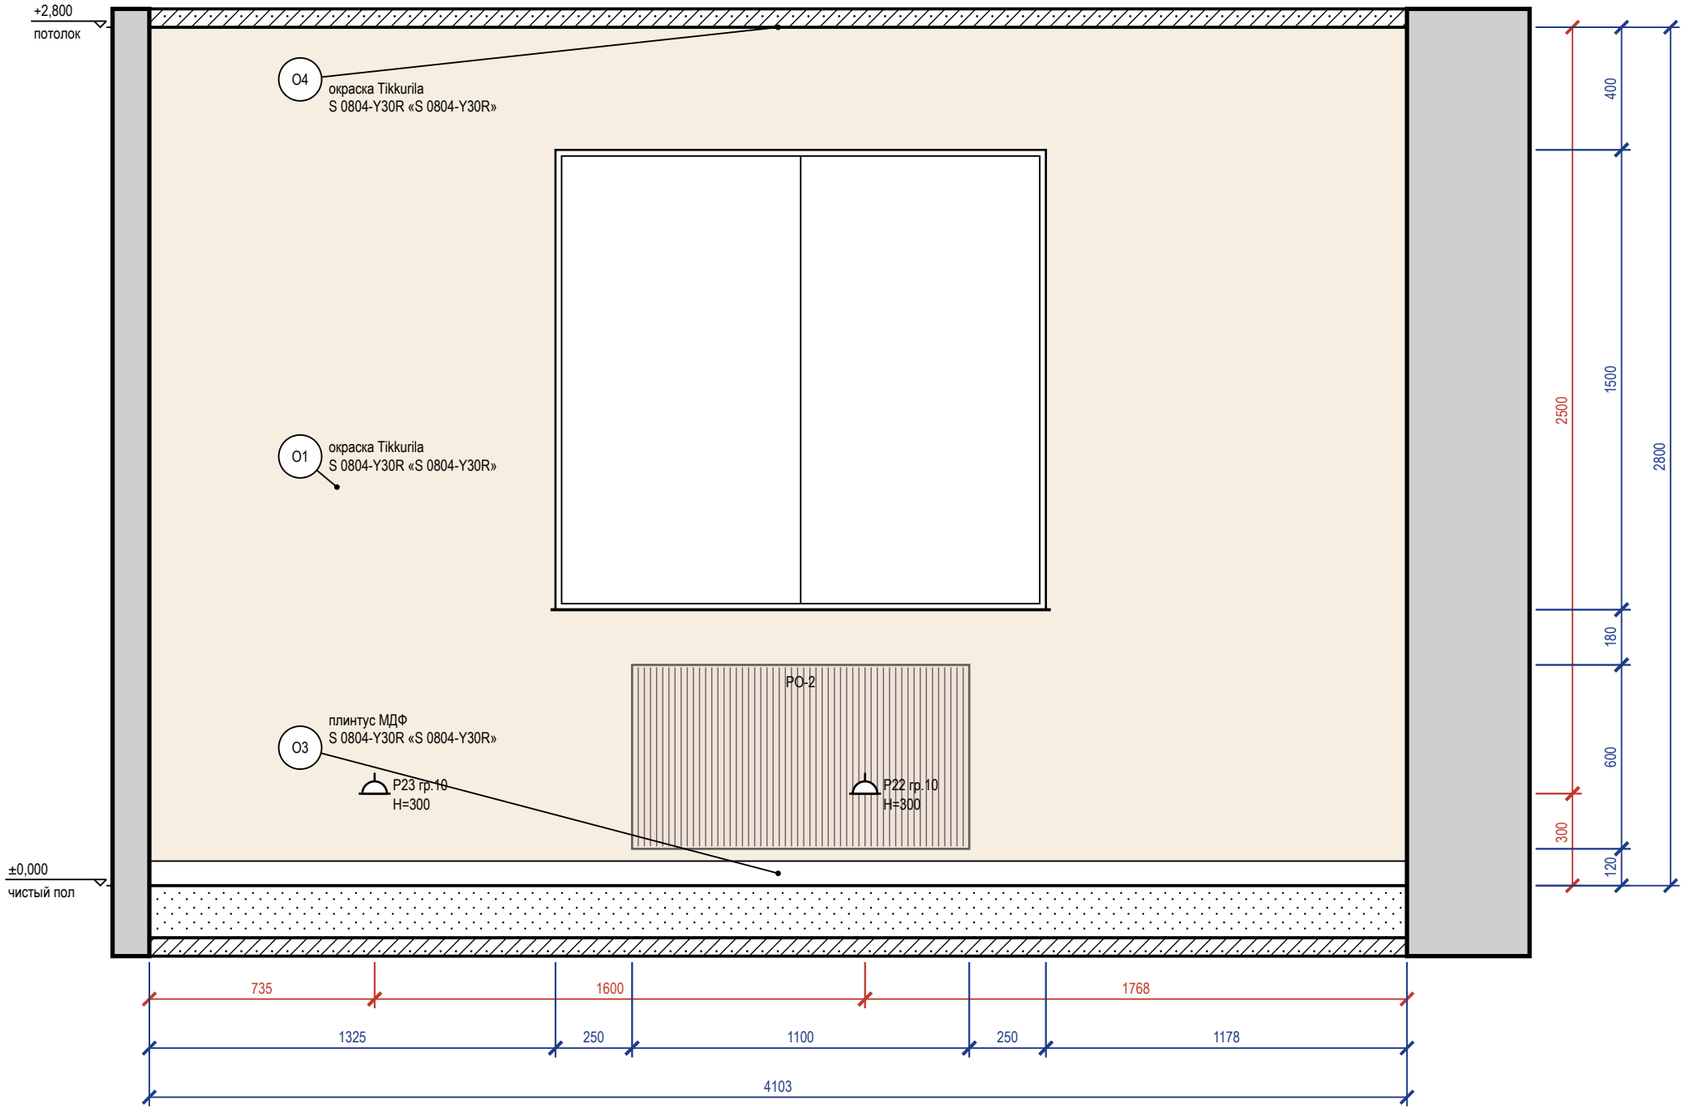


Схема развёрток (М 1:100)



Визуализация этой стены — лист 53

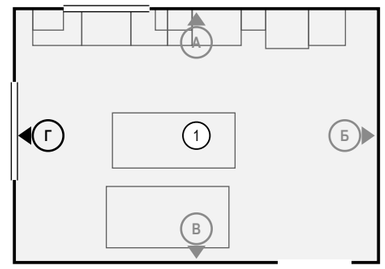

Ведомость отделки (на листе)

Марка	Поверхность	Материал, изделие	Цвет, код	Кол.
О1	стены	окраска, Tikkurila Luja 7, шелковисто-матовая, подготовка К3	NCS S 0804-Y30R «S 0804-Y30R»	9,1 м²
О3	плинтус	плинтус МДФ, h 80 мм, аналог: плинтус МДФ под окраску 80×16 мм, полуглянцевая	NCS S 0804-Y30R «S 0804-Y30R»	4,1 м
О4	потолок	окраска, Tikkurila Luja 7, матовая, подготовка Q3	NCS S 0804-Y30R «S 0804-Y30R»	24,6 м²

Примечания

1. Размеры — в мм от чистовых поверхностей стен; условные обозначения и общие указания — лист 2.

					Проект: Дом 331 м²
	Лист	№ док.	Подпись	Дата	Развёртка стены Г. Кухня-столовая (пом. 1)
Дизайнер	Кырлан А.С.			19.10.26	

Стадия	Лист	Листов
П	57	155

выпуск 18.10.2026 № ffc1f29499 · стр. 57 из 155



					Проект: Дом 331 м²
	Лист	№ док.	Подпись	Дата	
Дизайнер	Кырлан А.С.			19.10.26	Визуализация: Кабинет-гостевая

Стадия	Лист	Листов
П	58	155

выпуск 18.10.2026 № ffc1f29499 · стр. 58 из 155



					Проект: Дом 331 м²	
	Лист	№ док.	Подпись	Дата		
Дизайнер	Кырлан А.С.			19.10.26	Визуализация: Кабинет-гостевая	Стадия / Лист / Листов
						П / 59 / 155

выпуск 18.10.2026 № ffc1f29499 · стр. 59 из 155

Развёртка стены А


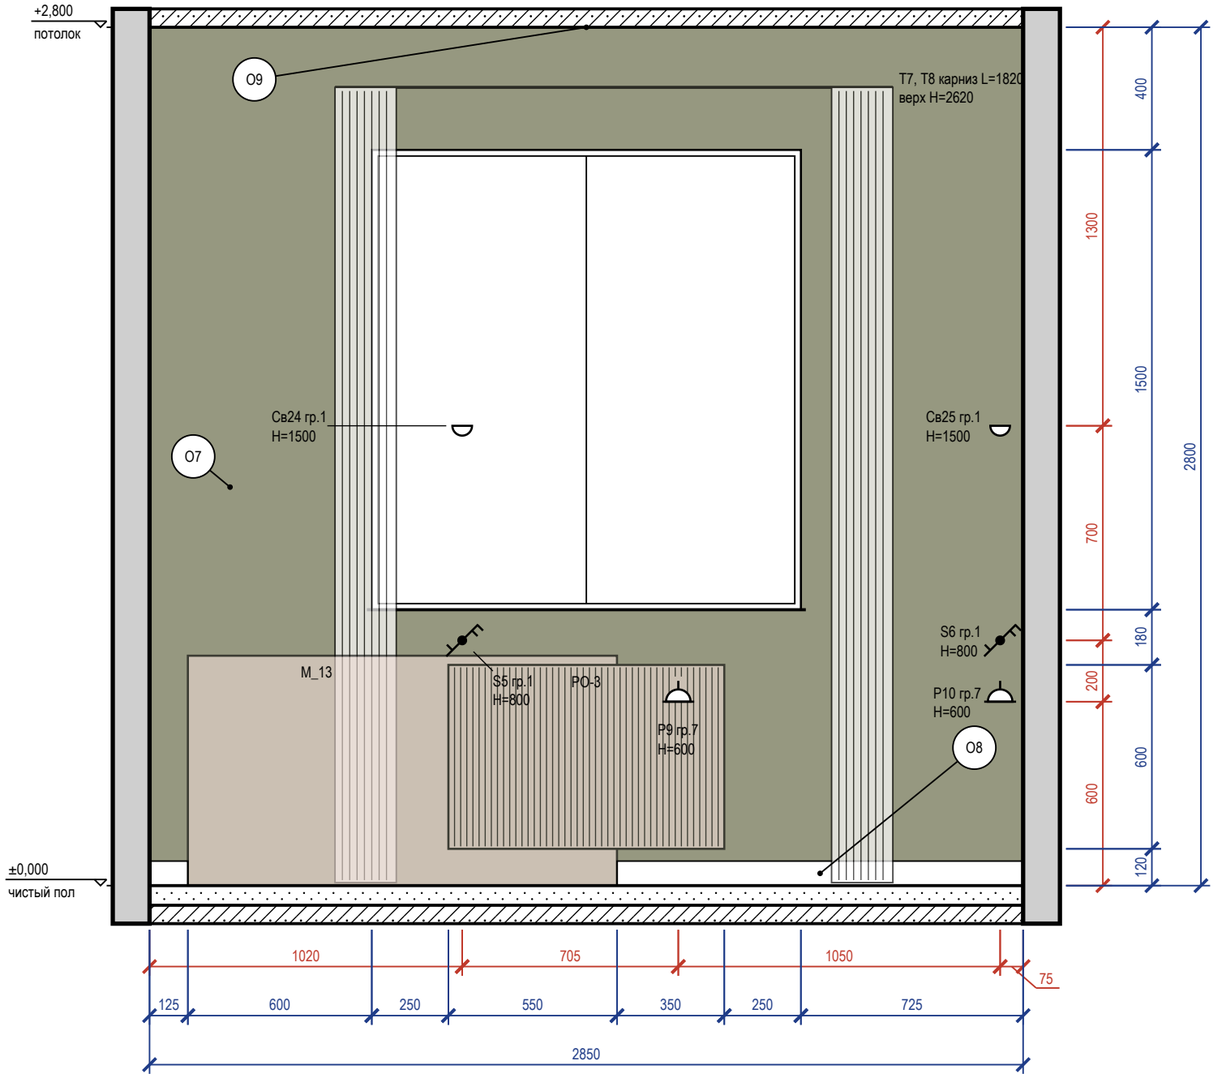


Схема развёрток (М 1:100)

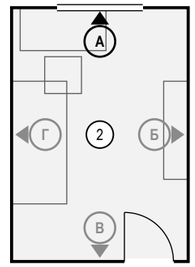

Ведомость отделки (на листе)

Марка	Поверхность	Материал, изделие	Цвет, код	Кол.
О7	акцентная стена	окраска, Farrow & Ball Modern Emulsion, матовая, подготовка Q3	Farrow & Ball No. 298 «Bancha»	5,9 м²
О8	плинтус	плинтус МДФ, h 80 мм, аналог: плинтус МДФ под покраску 80×16	Farrow & Ball No. 226 «Joa's White»	1,4 м
О9	потолок	окраска, Tikkurila Anti-Reflex 2, глубокоматовая, подготовка Q3	Little Greene No. 105 «Slaked Lime»	11,9 м²

Визуализация этой стены — лист 58



Примечания

1. Размеры — в мм от чистовых поверхностей стен; условные обозначения и общие указания — лист 2.
2. Карнизы (шины) — по ведомости текстиля декоратора; длина L и верх H — по развёртке, крепление — до окраски потолка.
3. Линии узора (швы плитки, складки штор, рёбра радиаторов) прерываются у знаков и выносок — просвет между линиями не менее 0,7 мм.

					Проект: Дом 331 м²
	Лист	№ док.	Подпись	Дата	Развёртка стены А. Кабинет-гостевая (пом. 2)
Дизайнер	Кырлан А.С.			19.10.26	

Стадия	Лист	Листов
П	60	155

выпуск 18.10.2026 № ffc1f29499 · стр. 60 из 155

Развёртка стены Б



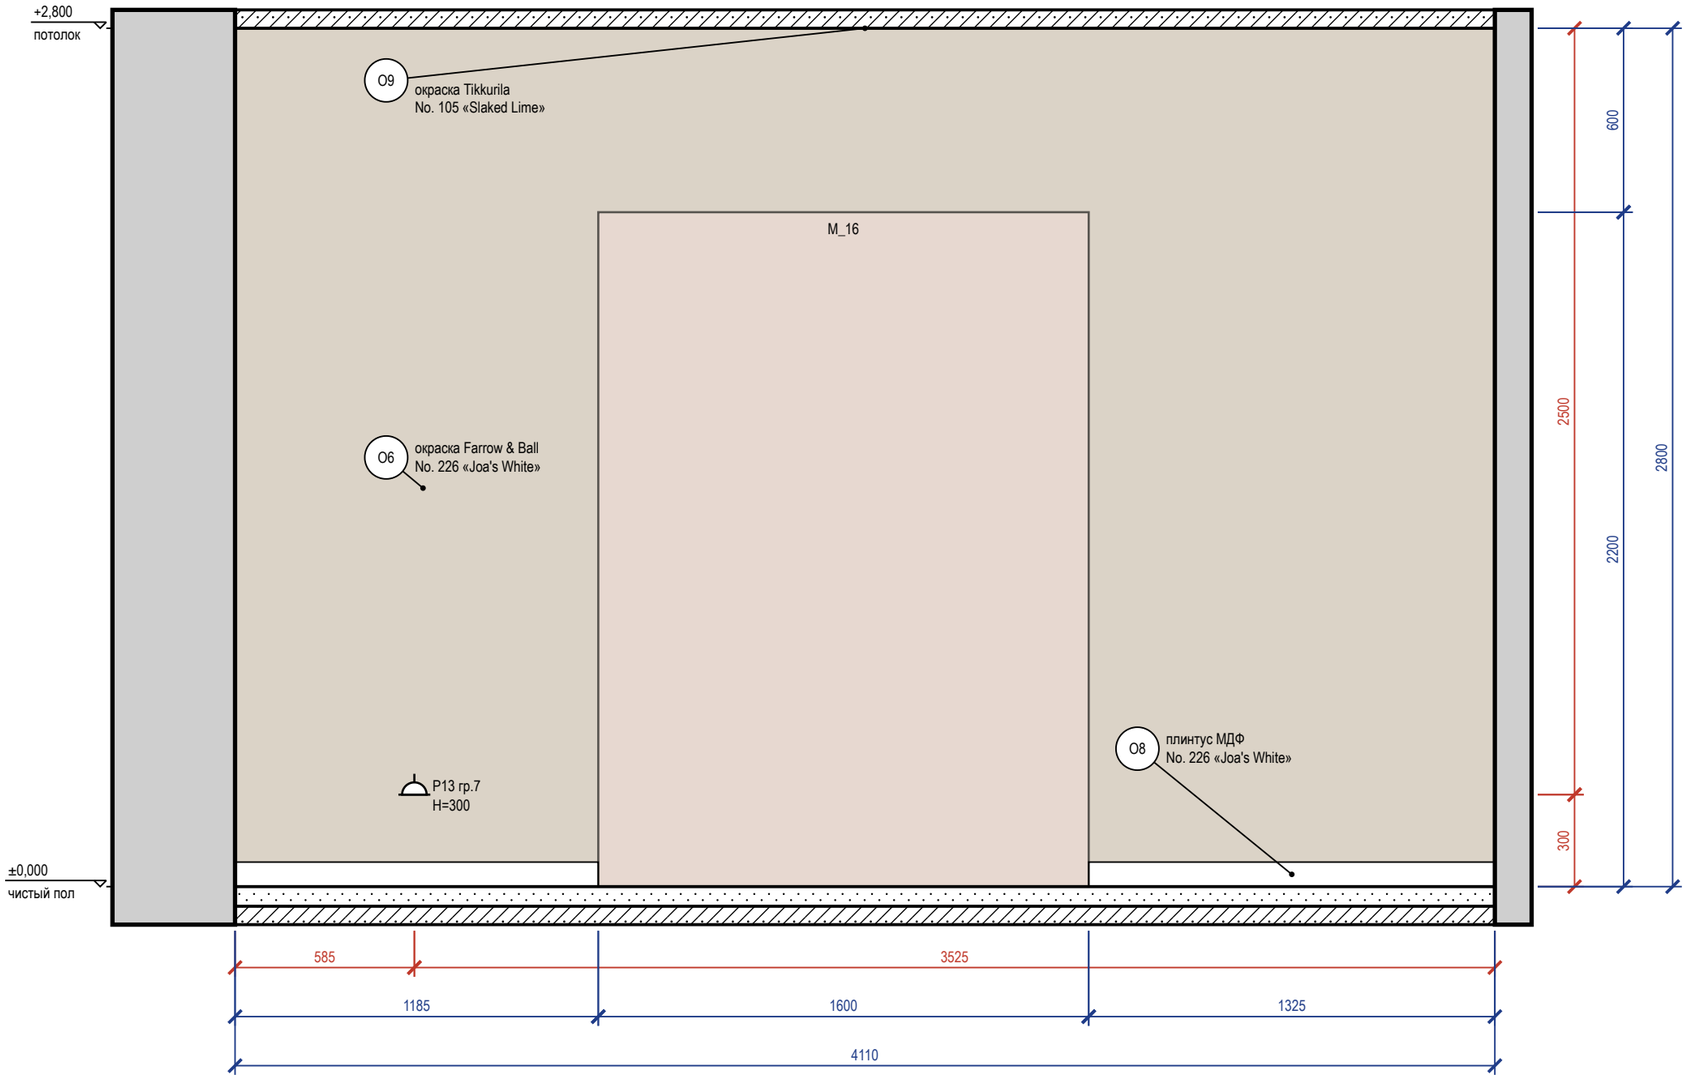


Схема развёрток (М 1:100)

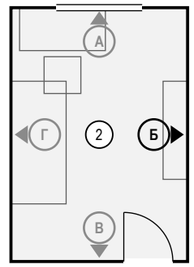

Визуализация этой стены

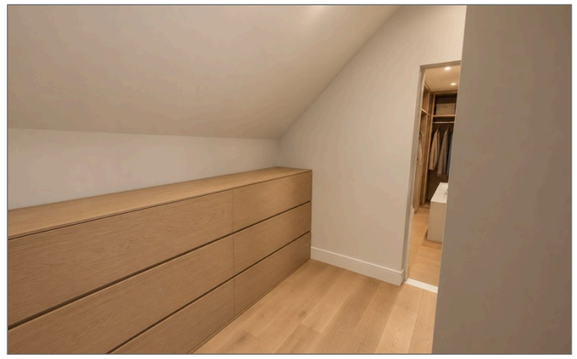

Ведомость отделки (на листе)

Марка	Поверхность	Материал, изделие	Цвет, код	Кол.
О6	стены	окраска, Farrow & Ball Modern Emulsion, матовая, подготовка Q3	Farrow & Ball No. 226 «Joa's White»	11,5 м²
О8	плинтус	плинтус МДФ, h 80 мм, аналог: плинтус МДФ под покраску 80×16	Farrow & Ball No. 226 «Joa's White»	2,5 м
О9	потолок	окраска, Tikkurila Anti-Reflex 2, глубокоматовая, подготовка Q3	Little Greene No. 105 «Slaked Lime»	11,9 м²

Примечания

1. Размеры — в мм от чистовых поверхностей стен; условные обозначения и общие указания — лист 2.

					Проект: Дом 331 м²
	Лист	№ док.	Подпись	Дата	Развёртка стены Б. Кабинет-гостевая (пом. 2)
Дизайнер	Кырлан А.С.			19.10.26	

Стадия	Лист	Листов
П	61	155

выпуск 18.10.2026 № ffc1f29499 · стр. 61 из 155

Развёртка стены В


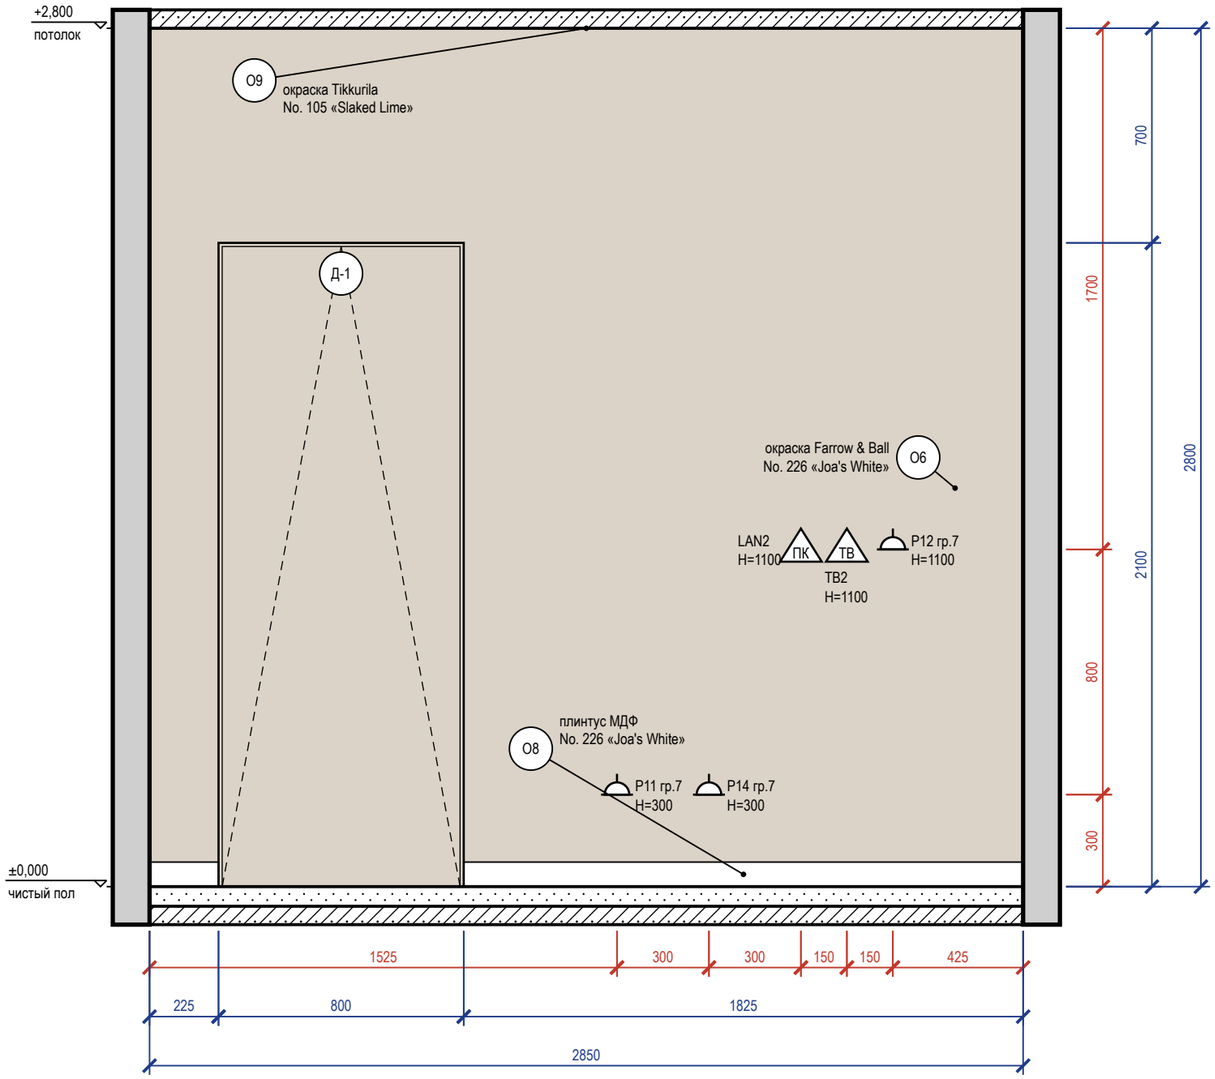


Схема развёрток (М 1:100)

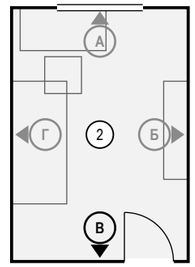

Ведомость отделки (на листе)

Марка	Поверхность	Материал, изделие	Цвет, код	Кол.
О6	стены	окраска, Farrow & Ball Modern Emulsion, матовая, подготовка Q3	Farrow & Ball No. 226 «Joa's White»	6,3 м²
О8	плинтус	плинтус МДФ, h 80 мм, аналог: плинтус МДФ под покраску 80×16	Farrow & Ball No. 226 «Joa's White»	2 м
О9	потолок	окраска, Tikkurila Anti-Reflex 2, глубокоматовая, подготовка Q3	Little Greene No. 105 «Slaked Lime»	11,9 м²

Примечания

1. Размеры — в мм от чистовых поверхностей стен; условные обозначения и общие указания — лист 2.
2. Двери скрытого монтажа — полотно в плоскости стены, отделка стены по полотну, плинтус прерывается у короба (узел — на листе узлов).

					Проект: Дом 331 м²
	Лист	№ док.	Подпись	Дата	Развёртка стены В. Кабинет-гостевая (пом. 2)
Дизайнер	Кырлан А.С.			19.10.26	

Стадия	Лист	Листов
П	62	155

выпуск 18.10.2026 № ffc1f29499 · стр. 62 из 155

Развёртка стены Г


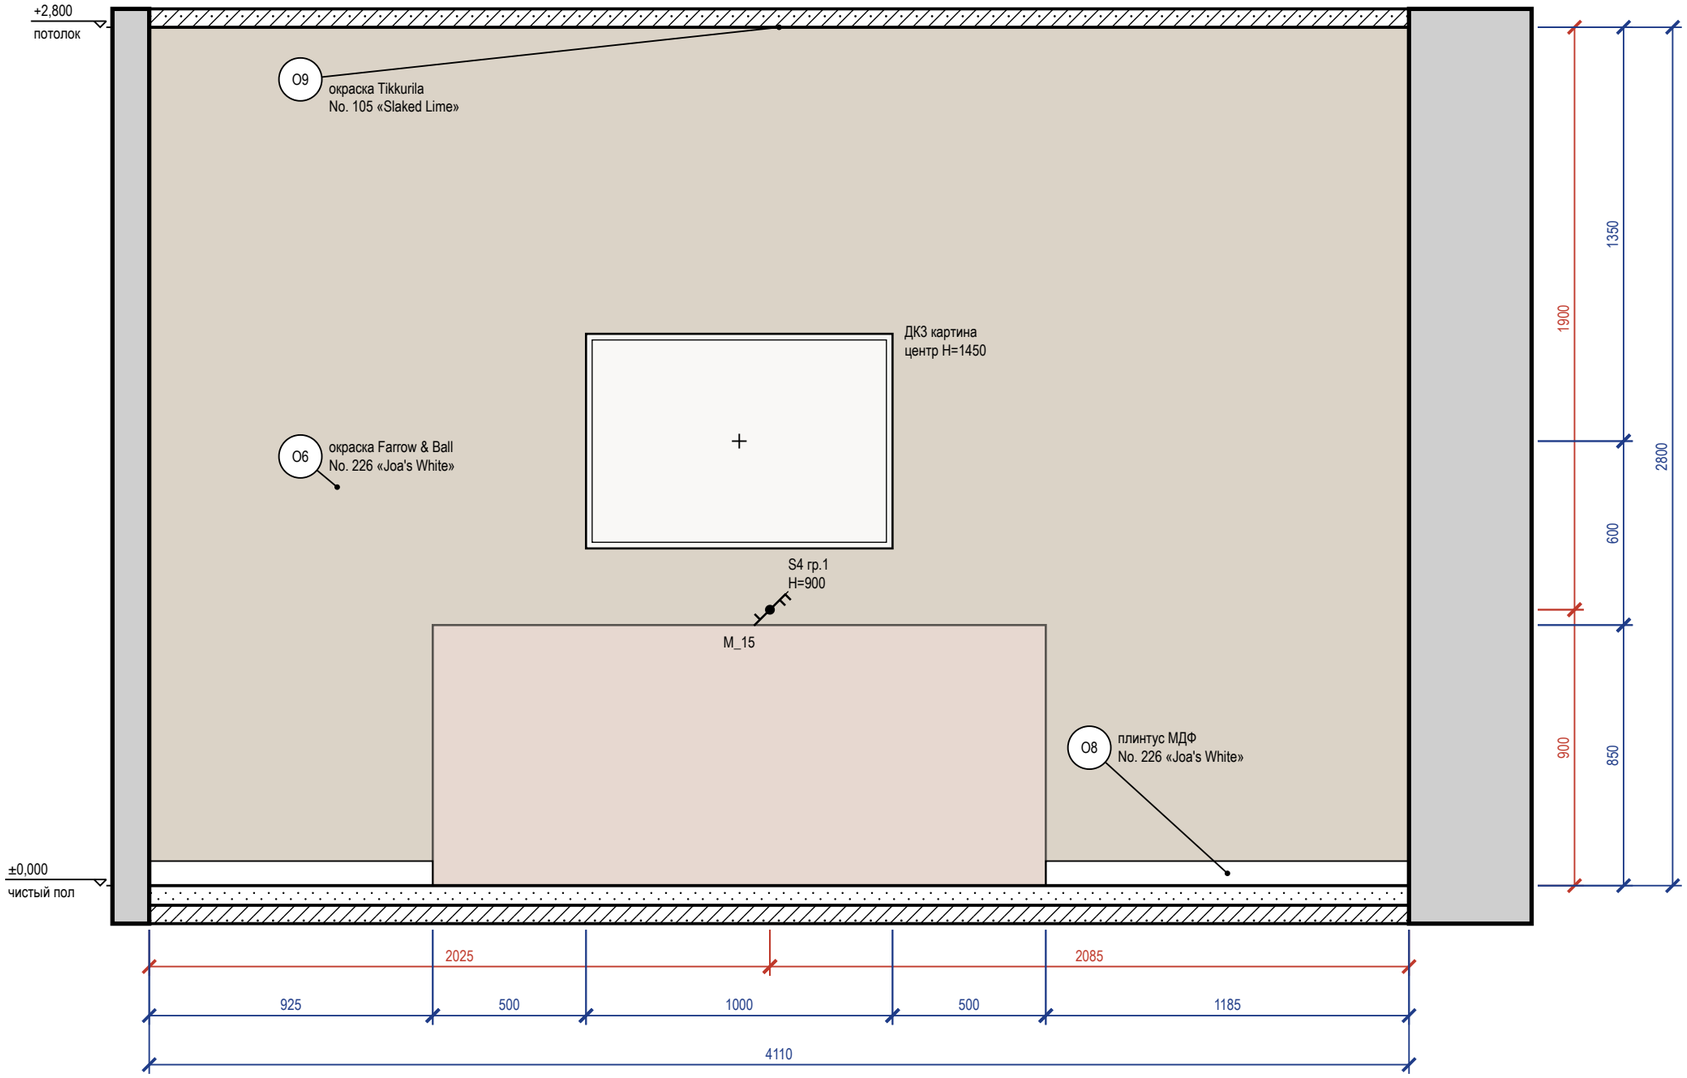


Схема развёрток (М 1:100)



Визуализация этой стены — лист 59

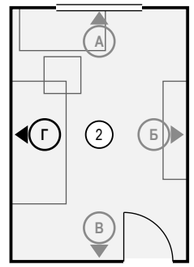

Ведомость отделки (на листе)

Марка	Поверхность	Материал, изделие	Цвет, код	Кол.
О6	стены	окраска, Farrow & Ball Modern Emulsion, матовая, подготовка Q3	Farrow & Ball No. 226 «Joa's White»	11,5 м²
О8	плинтус	плинтус МДФ, h 80 мм, аналог: плинтус МДФ под покраску 80×16	Farrow & Ball No. 226 «Joa's White»	2,1 м
О9	потолок	окраска, Tikkurila Anti-Reflex 2, глубокоматовая, подготовка Q3	Little Greene No. 105 «Slaked Lime»	11,9 м²

Примечания

1. Размеры — в мм от чистовых поверхностей стен; условные обозначения и общие указания — лист 2.
2. Картины и зеркала крепить к основанию по паспорту изделия (закладные и анкеры — в перечне скрытых работ); крест — ось центра предмета.

					Проект: Дом 331 м²
	Лист	№ док.	Подпись	Дата	Развёртка стены Г. Кабинет-гостевая (пом. 2)
Дизайнер	Кырлан А.С.			19.10.26	

Стадия	Лист	Листов
П	63	155

выпуск 18.10.2026 · ffc1f29499 · стр. 63 из 155



					Проект: Дом 331 м²	
	Лист	№ док.	Подпись	Дата	Визуализация: Санузел 1 этажа	Стадия / Лист / Листов
Дизайнер	Кырлан А.С.			19.10.26		П / 64 / 155

выпуск 18.10.2026 № ffc1f29499 · стр. 64 из 155

Развёртка стены А


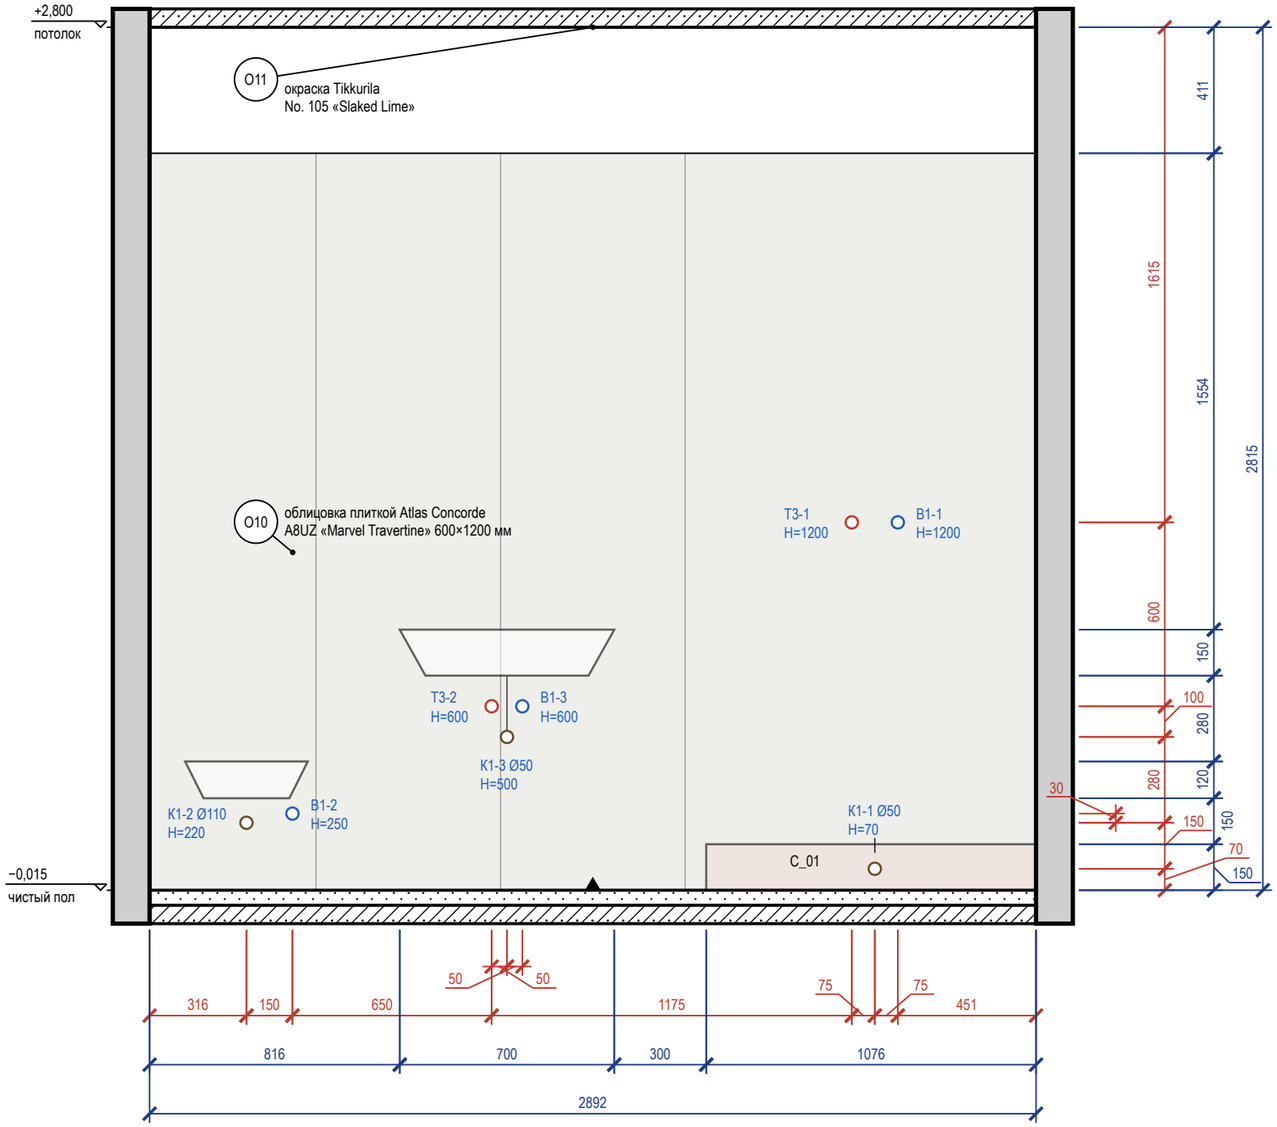


Схема развёрток (М 1:100)

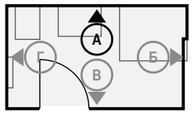

Ведомость отделки (на листе)

Марка	Поверхность	Материал, изделие	Цвет, код	Кол.
O10	стены	облицовка плиткой, Atlas Concorde Marvel Travertine, 600×1200×9 мм, A8UZ, затирка CG2WA	Atlas Concorde A8UZ «Marvel Travertine»	7 м²
O11	потолок	окраска, Tikkurila Luja 7, матовая, подготовка Q3	Little Greene No. 105 «Slaked Lime»	4,9 м²

Визуализация этой стены




Примечания

1. Размеры — в мм от чистовых поверхностей стен; условные обозначения и общие указания — лист 2.
2. Схема мебели, приборов и декора не является технической документацией для производства мебели; габариты — по паспортам изделий.
3. Выводы ВК — коды и высоты по листу выводов сантехники.
4. Облицовка — по сетке швов 2 мм, раскладка от оси стены (треугольник у пола), целые ряды от пола; подрезки — по листу раскладки плитки.
5. Гидроизоляция в 2 слоя, заход на стены 200 мм — до облицовки, с актом скрытых работ и тестом проливом (узел — на листе узлов).

					Проект: Дом 331 м²
	Лист	№ док.	Подпись	Дата	Развёртка стены А. Санузел 1 этажа (пом. 3)
Дизайнер	Кырлан А.С.			19.10.26	

Стадия	Лист	Листов
П	65	155

Развёртка стены Б

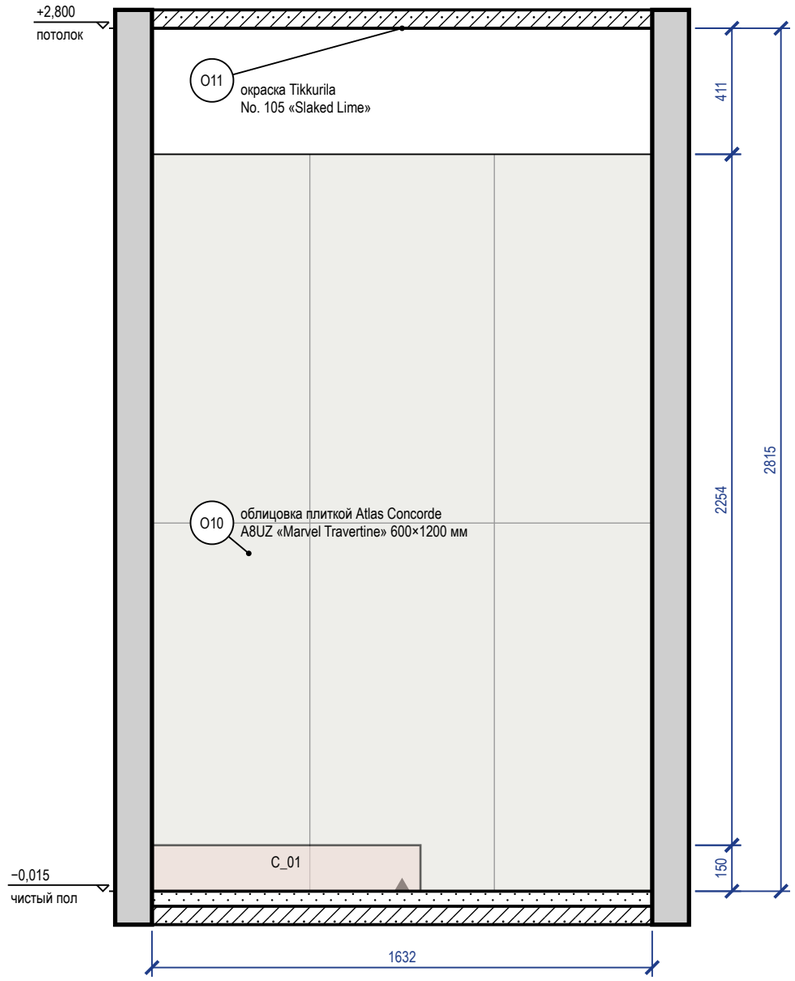

Развёртка стены В


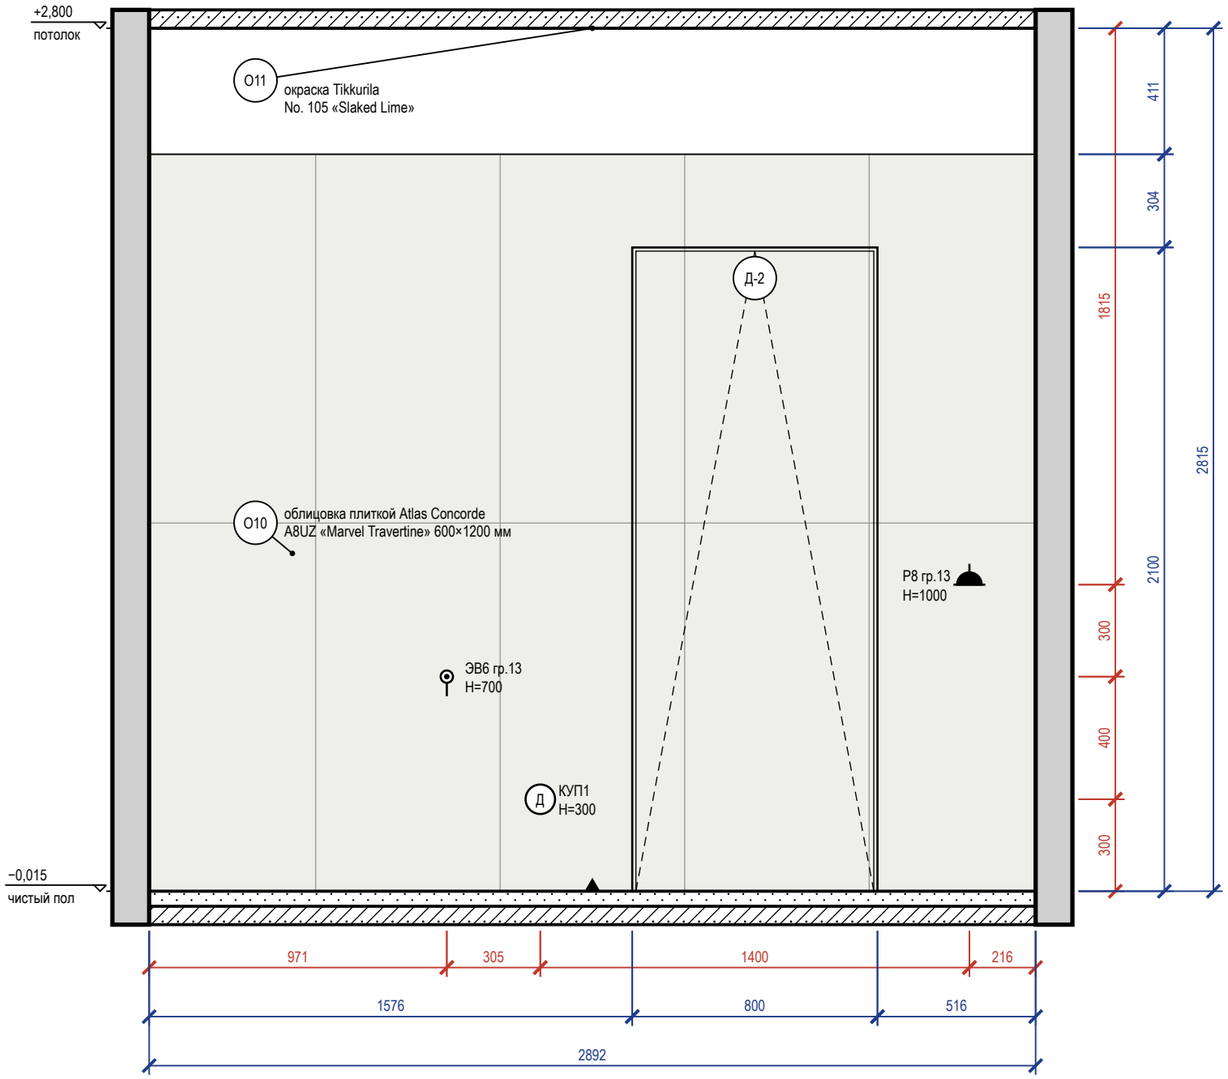



Схема развёрток (М 1:100)

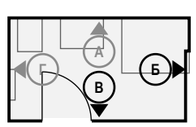

Ведомость отделки (на листе)

Марка	Поверхность	Материал, изделие	Цвет, код	Кол.
О10	стены	облицовка плиткой, Atlas Concorde Marvel Travertine, 600×1200×9 мм, A8UZ, затирка CG2WA	Atlas Concorde A8UZ «Marvel Travertine»	9,2 м²
О11	потолок	окраска, Tikkurila Luja 7, матовая, подготовка Q3	Little Greene No. 105 «Slaked Lime»	4,9 м²

Визуализация этой стены — лист 64

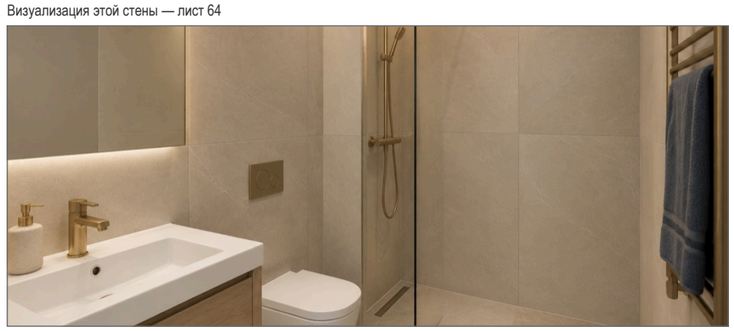

Примечания

1. Размеры — в мм от чистовых поверхностей стен; условные обозначения и общие указания — лист 2.
2. Схема мебели, приборов и декора не является технической документацией для производства мебели; габариты — по паспортам изделий.
3. Облицовка — по сетке швов 2 мм, раскладка от оси стены (треугольник у пола), целые ряды от пола; подрезки — по листу раскладки плитки.
4. Гидроизоляция в 2 слоя, заход на стены 200 мм — до облицовки, с актом скрытых работ и тестом проливом (узел — на листе узлов).
5. Двери скрытого монтажа — полотно в плоскости стены, отделка стены по полотну, плинтус прерывается у короба (узел — на листе узлов).

					Проект: Дом 331 м²
	Лист	№ док.	Подпись	Дата	Развёртки стен Б, В. Санузел 1 этажа (пом. 3)
Дизайнер	Кырлан А.С.			19.10.26	

Стадия	Лист	Листов
П	66	155

выпуск 18.10.2026 № ffc1f29499 · стр. 66 из 155

Развёртка стены Г


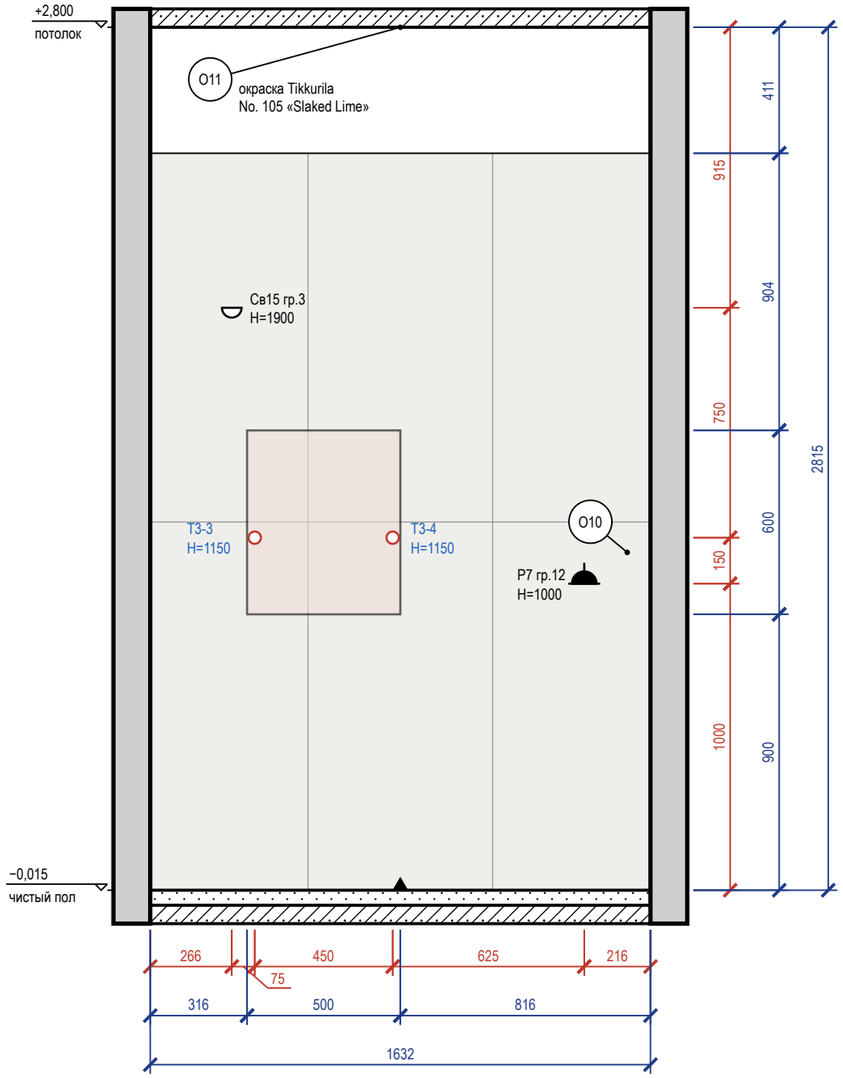


Схема развёрток (М 1:100)

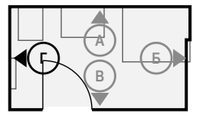

Ведомость отделки (на листе)

Марка	Поверхность	Материал, изделие	Цвет, код	Кол.
О10	стены	облицовка плиткой, Atlas Concorde Marvel Travertine, 600×1200×9 мм, A8UZ, затирка CG2WA	Atlas Concorde A8UZ «Marvel Travertine»	3,9 м²
О11	потолок	окраска, Tikkurila Luja 7, матовая, подготовка Q3	Little Greene No. 105 «Slaked Lime»	4,9 м²

Примечания

1. Размеры — в мм от чистовых поверхностей стен; условные обозначения и общие указания — лист 2.
2. Схема мебели, приборов и декора не является технической документацией для производства мебели; габариты — по паспортам изделий.
3. Выводы ВК — коды и высоты по листу выводов сантехники.
4. Облицовка — по сетке швов 2 мм, раскладка от оси стены (треугольник у пола), целые ряды от пола; подрезки — по листу раскладки плитки.
5. Гидроизоляция в 2 слоя, заход на стены 200 мм — до облицовки, с актом скрытых работ и тестом проливом (узел — на листе узлов).

					Проект: Дом 331 м²
	Лист	№ док.	Подпись	Дата	Развёртка стены Г. Санузел 1 этажа (пом. 3)
Дизайнер	Кырлан А.С.			19.10.26	

Стадия	Лист	Листов
П	67	155

выпуск 18.10.2026 № ffc1f29499 · стр. 67 из 155



					Проект: Дом 331 м²
	Лист	№ док.	Подпись	Дата	
Дизайнер	Кырлан А.С.			19.10.26	Визуализация: Котельная

Стадия	Лист	Листов
П	68	155

выпуск 18.10.2026 № ffc1f29499 · стр. 68 из 155

Развёртка стены А


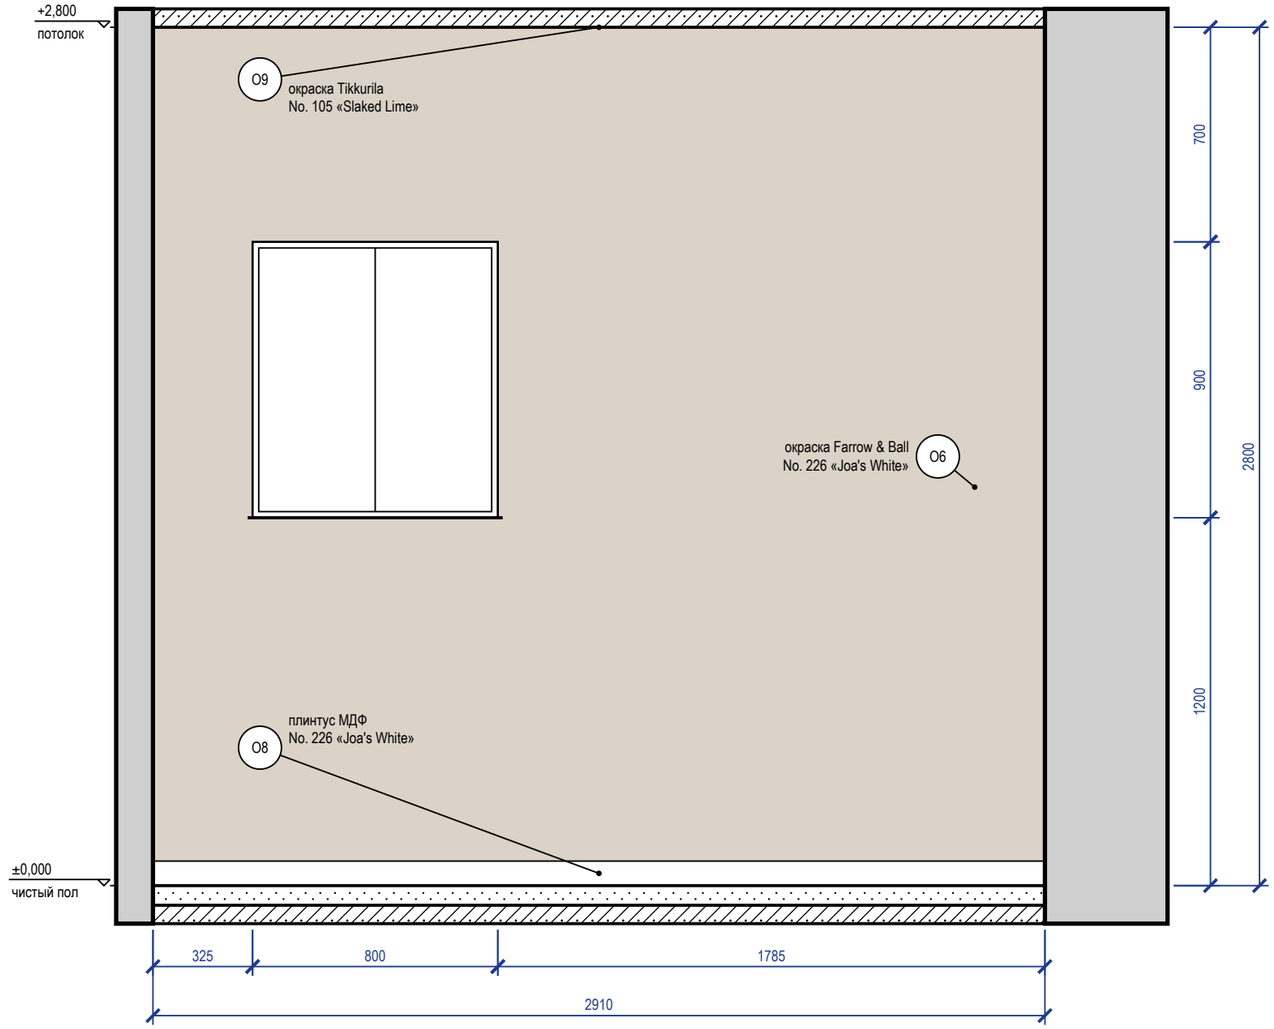


Схема развёрток (М 1:100)

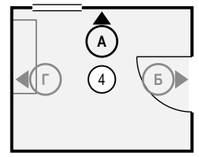

Ведомость отделки (на листе)

Марка	Поверхность	Материал, изделие	Цвет, код	Кол.
О6	стены	окраска, Farrow & Ball Modern Emulsion, матовая, подготовка Q3	Farrow & Ball No. 226 «Joa's White»	7,4 м²
О8	плинтус	плинтус МДФ, h 80 мм, аналог: плинтус МДФ под покраску 80×16	Farrow & Ball No. 226 «Joa's White»	2,9 м
О9	потолок	окраска, Tikkurila Anti-Reflex 2, глубокоматовая, подготовка Q3	Little Greene No. 105 «Slaked Lime»	6,9 м²

Примечания


1. Размеры — в мм от чистовых поверхностей стен; условные обозначения и общие указания — лист 2.

					Проект: Дом 331 м²
	Лист	№ док.	Подпись	Дата	Развёртка стены А. Котельная (пом. 4)
Дизайнер	Кырлан А.С.			19.10.26	

Стадия	Лист	Листов
П	69	155

выпуск 18.10.2026 № ffc1f29499 · стр. 69 из 155

Развёртка стены Б

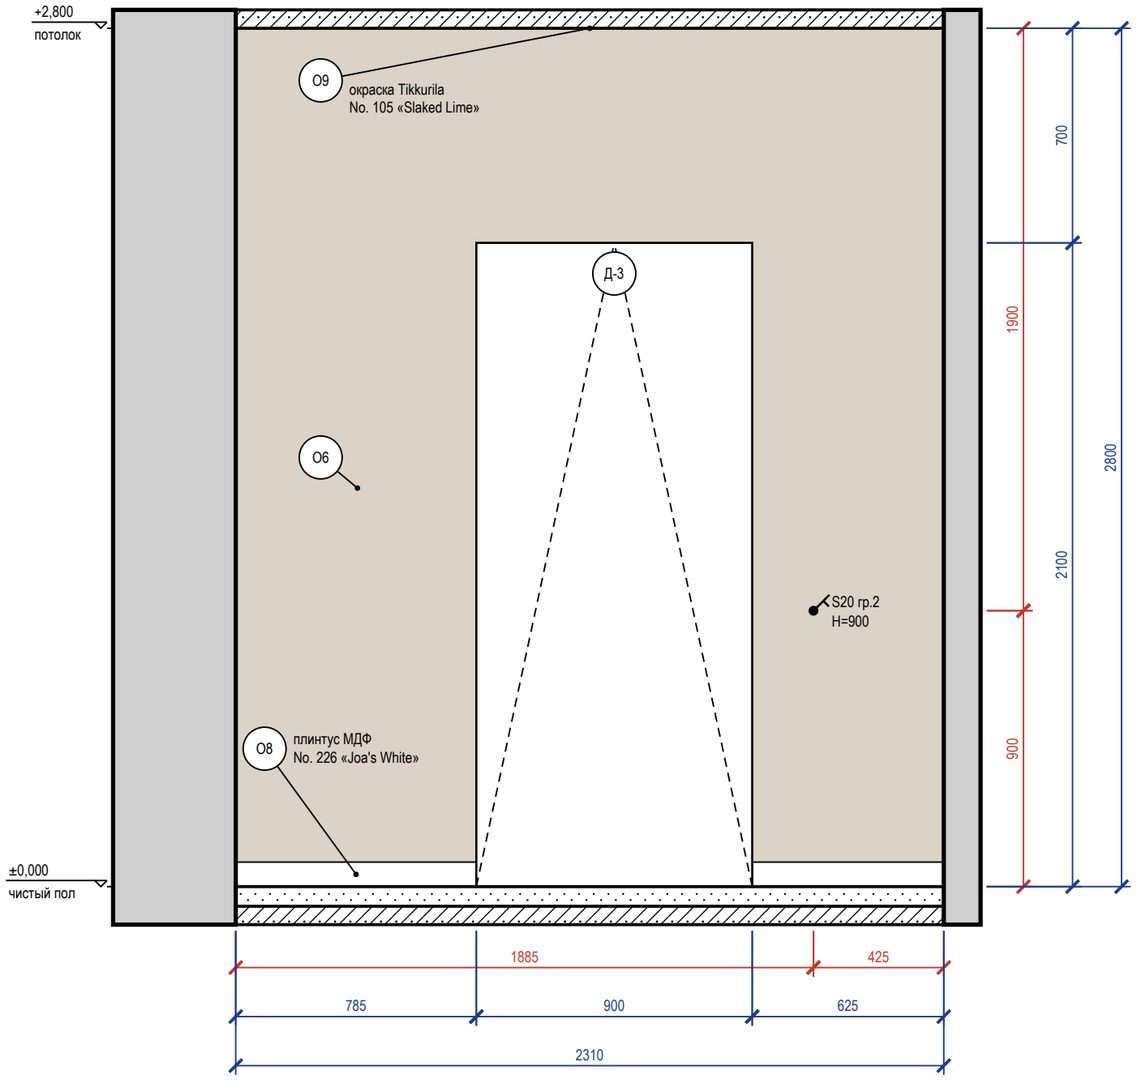

Развёртка стены Г


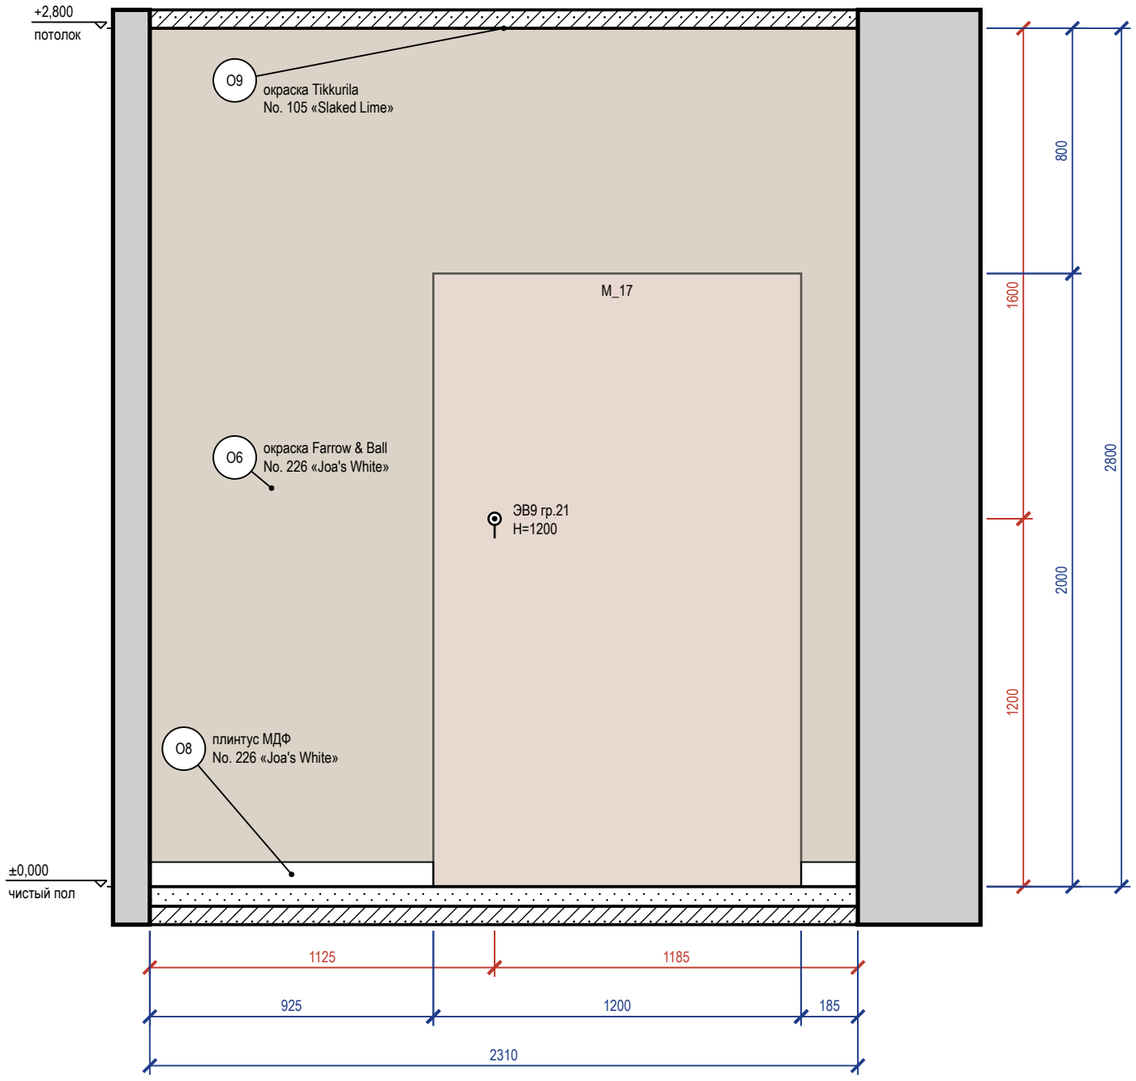


Схема развёрток (М 1:100)

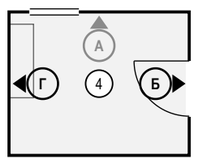

Ведомость отделки (на листе)

Марка	Поверхность	Материал, изделие	Цвет, код	Кол.
О6	стены	окраска, Farrow & Ball Modern Emulsion, матовая, подготовка Q3	Farrow & Ball No. 226 «Joa's White»	11 м²
О8	плинтус	плинтус МДФ, h 80 мм, аналог: плинтус МДФ под покраску 80×16	Farrow & Ball No. 226 «Joa's White»	2,5 м
О9	потолок	окраска, Tikkurila Anti-Reflex 2, глубокоматовая, подготовка Q3	Little Greene No. 105 «Slaked Lime»	6,9 м²

Визуализация этой стены



Примечания

1. Размеры — в мм от чистовых поверхностей стен; условные обозначения и общие указания — лист 2.

					Проект: Дом 331 м²
	Лист	№ док.	Подпись	Дата	Развёртки стен Б, Г. Котельная (пом. 4)
Дизайнер	Кырлан А.С.			19.10.26	

Стадия	Лист	Листов
П	70	155

выпуск 18.10.2026 № ffc1f29499 · стр. 70 из 155



					Проект: Дом 331 м²
	Лист	№ док.	Подпись	Дата	
Дизайнер	Кырлан А.С.			19.10.26	Визуализация гостиной

Стадия	Лист	Листов
П	71	155

выпуск 18.10.2026 · ffc1f29499 · стр. 71 из 155



					Проект: Дом 331 м²
	Лист	№ док.	Подпись	Дата	
Дизайнер	Кырлан А.С.			19.10.26	Визуализация гостиной

Стадия	Лист	Листов
П	72	155

выпуск 18.10.2026 № ffc1f29499 · стр. 72 из 155



					Проект: Дом 331 м²
	Лист	№ док.	Подпись	Дата	Визуализация гостиной
Дизайнер	Кырлан А.С.			19.10.26	

Стадия	Лист	Листов
П	73	155

выпуск 18.10.2026 № ffc1f29499 · стр. 73 из 155

Развёртка стены А


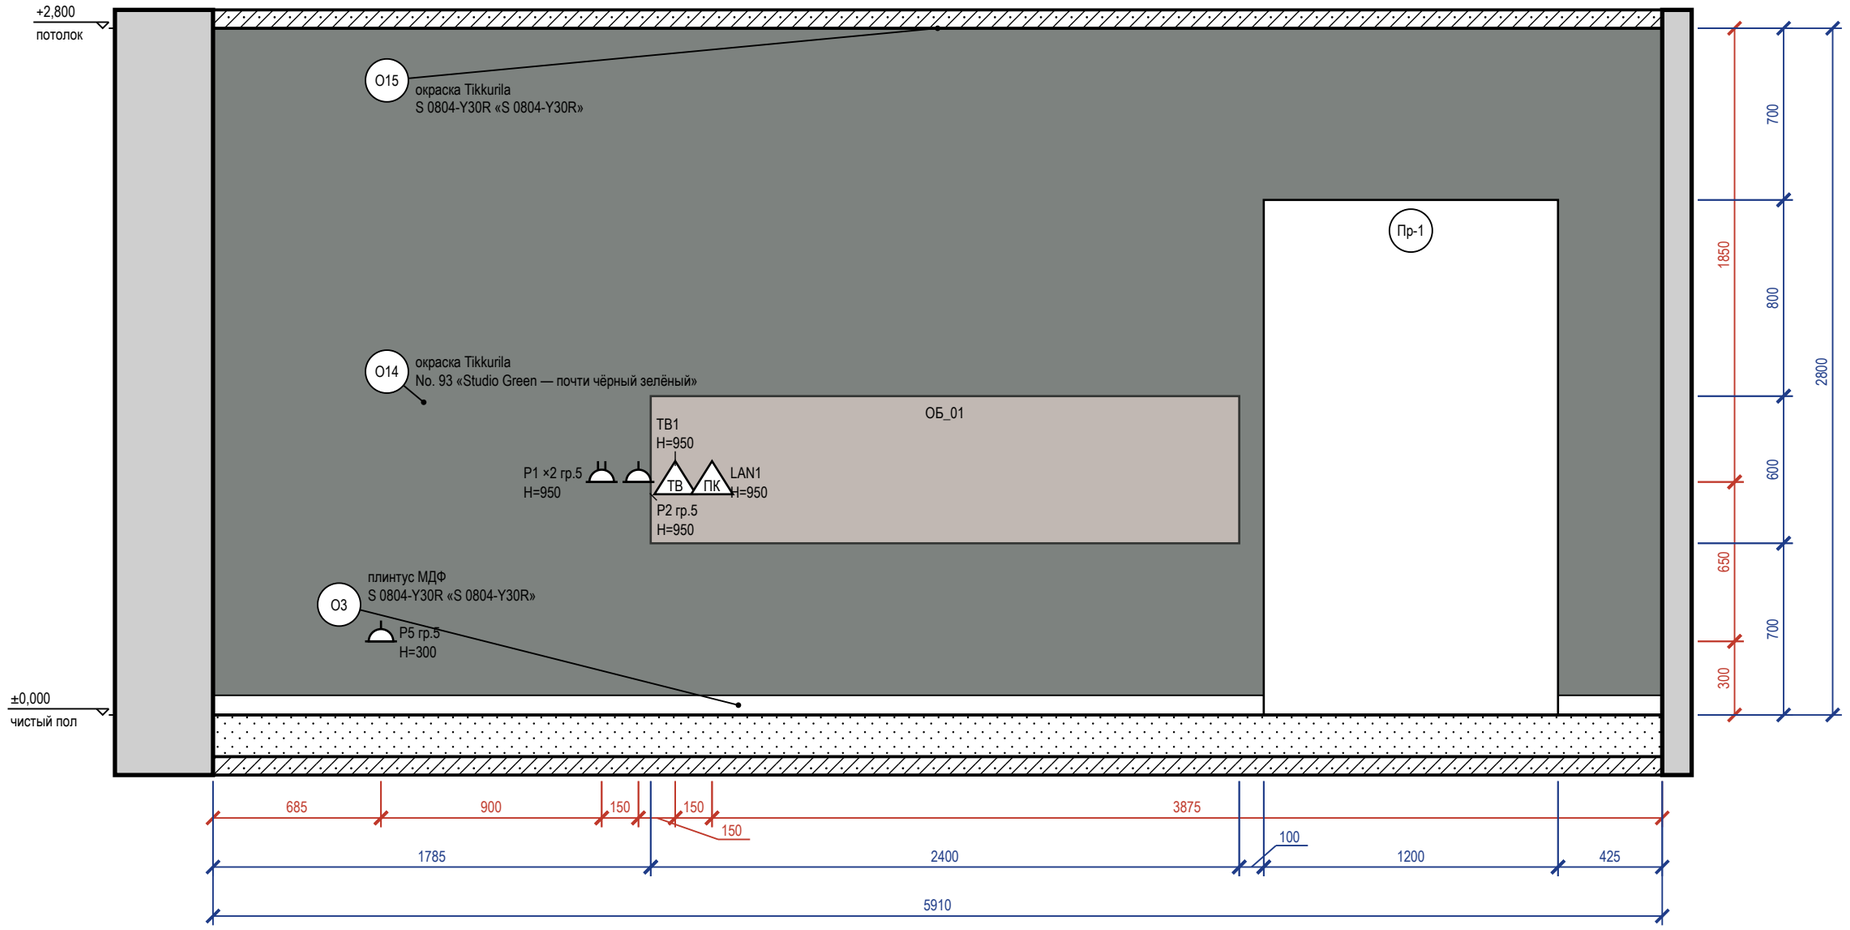


Схема развёрток (М 1:100)

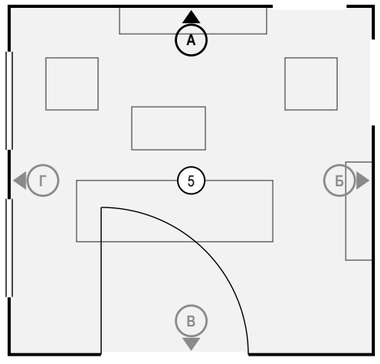

Ведомость отделки (на листе)

Марка	Поверхность	Материал, изделие	Цвет, код	Кол.
О3	плинтус	плинтус МДФ, h 80 мм, аналог: плинтус МДФ под окраску 80×16 мм, полуглянцевая	NCS S 0804-Y30R «S 0804-Y30R»	4,7 м
О14	акцентная стена	окраска, Tikkurila Optiva 5 Matt, аналог: интерьерная краска, класс 2 по EN 13300, глубокоматовая/матовая, база С, матовая, подготовка К3	Farrow & Ball No. 93 «Studio Green — почти чёрный зелёный»	14 м²
О15	потолок	окраска, Tikkurila Anti-Reflex 2, глубокоматовая, подготовка Q3	NCS S 0804-Y30R «S 0804-Y30R»	33,7 м²

Визуализация этой стены — лист 71



Примечания

1. Размеры — в мм от чистовых поверхностей стен; условные обозначения и общие указания — лист 2.
2. Схема мебели, приборов и декора не является технической документацией для производства мебели; габариты — по паспортам изделий.

					Проект: Дом 331 м²
	Лист	№ док.	Подпись	Дата	Развёртка стены А. Гостиная (пом. 5)
Дизайнер	Кырлан А.С.			19.10.26	

Стадия	Лист	Листов
П	74	155

выпуск 18.10.2026 № ffc1f29499 · стр. 74 из 155

Развёртка стены Б


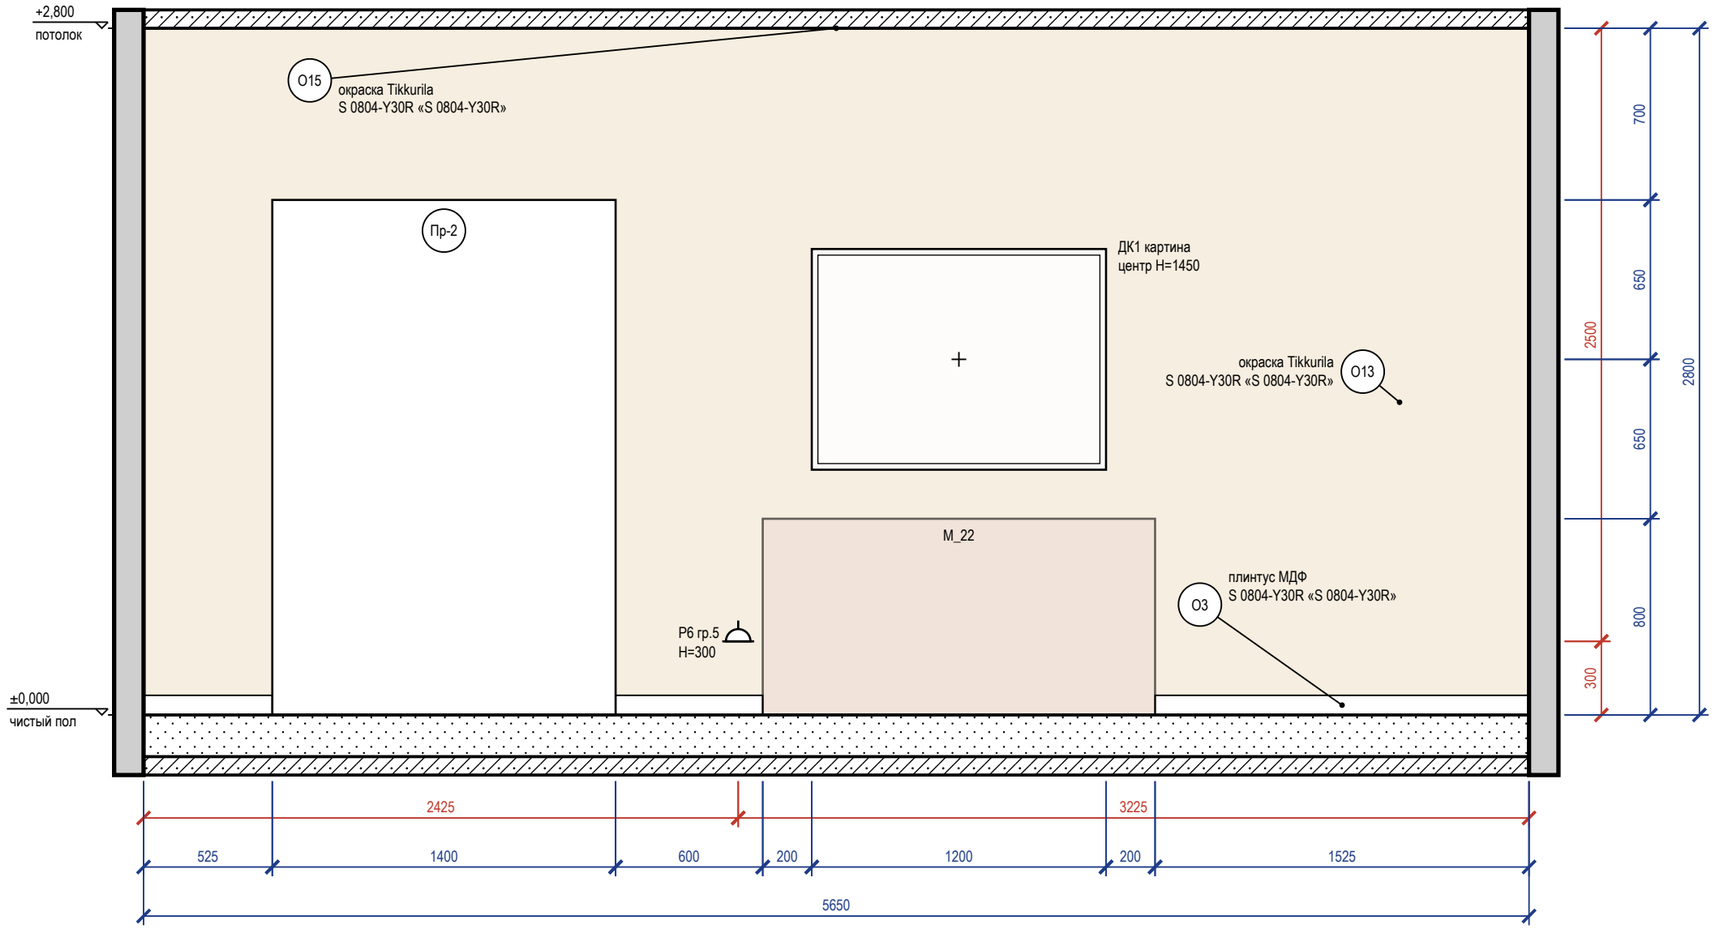


Схема развёрток (М 1:100)

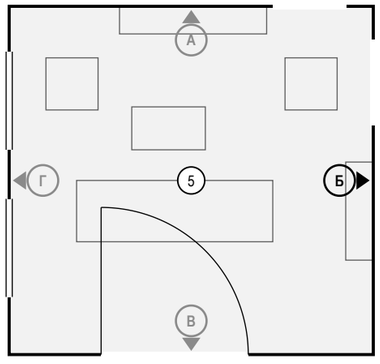

Ведомость отделки (на листе)

Марка	Поверхность	Материал, изделие	Цвет, код	Кол.
О3	плинтус	плинтус МДФ, h 80 мм, аналог: плинтус МДФ под окраску 80×16 мм, полуглянцевая	NCS S 0804-Y30R «S 0804-Y30R»	2,6 м
О13	стены	окраска, Tikkurila Optiva 5 Matt, матовая, подготовка К3	NCS S 0804-Y30R «S 0804-Y30R»	12,9 м²
О15	потолок	окраска, Tikkurila Anti-Reflex 2, глубокоматовая, подготовка Q3	NCS S 0804-Y30R «S 0804-Y30R»	33,7 м²

Примечания

1. Размеры — в мм от чистовых поверхностей стен; условные обозначения и общие указания — лист 2.
2. Картины и зеркала крепить к основанию по паспорту изделия (закладные и анкеры — в перечне скрытых работ); крест — ось центра предмета.

					Проект: Дом 331 м²
	Лист	№ док.	Подпись	Дата	Развёртка стены Б. Гостиная (пом. 5)
Дизайнер	Кырлан А.С.			19.10.26	

Стадия	Лист	Листов
П	75	155

выпуск 18.10.2026 № ffc1f29499 · стр. 75 из 155

Развёртка стены В


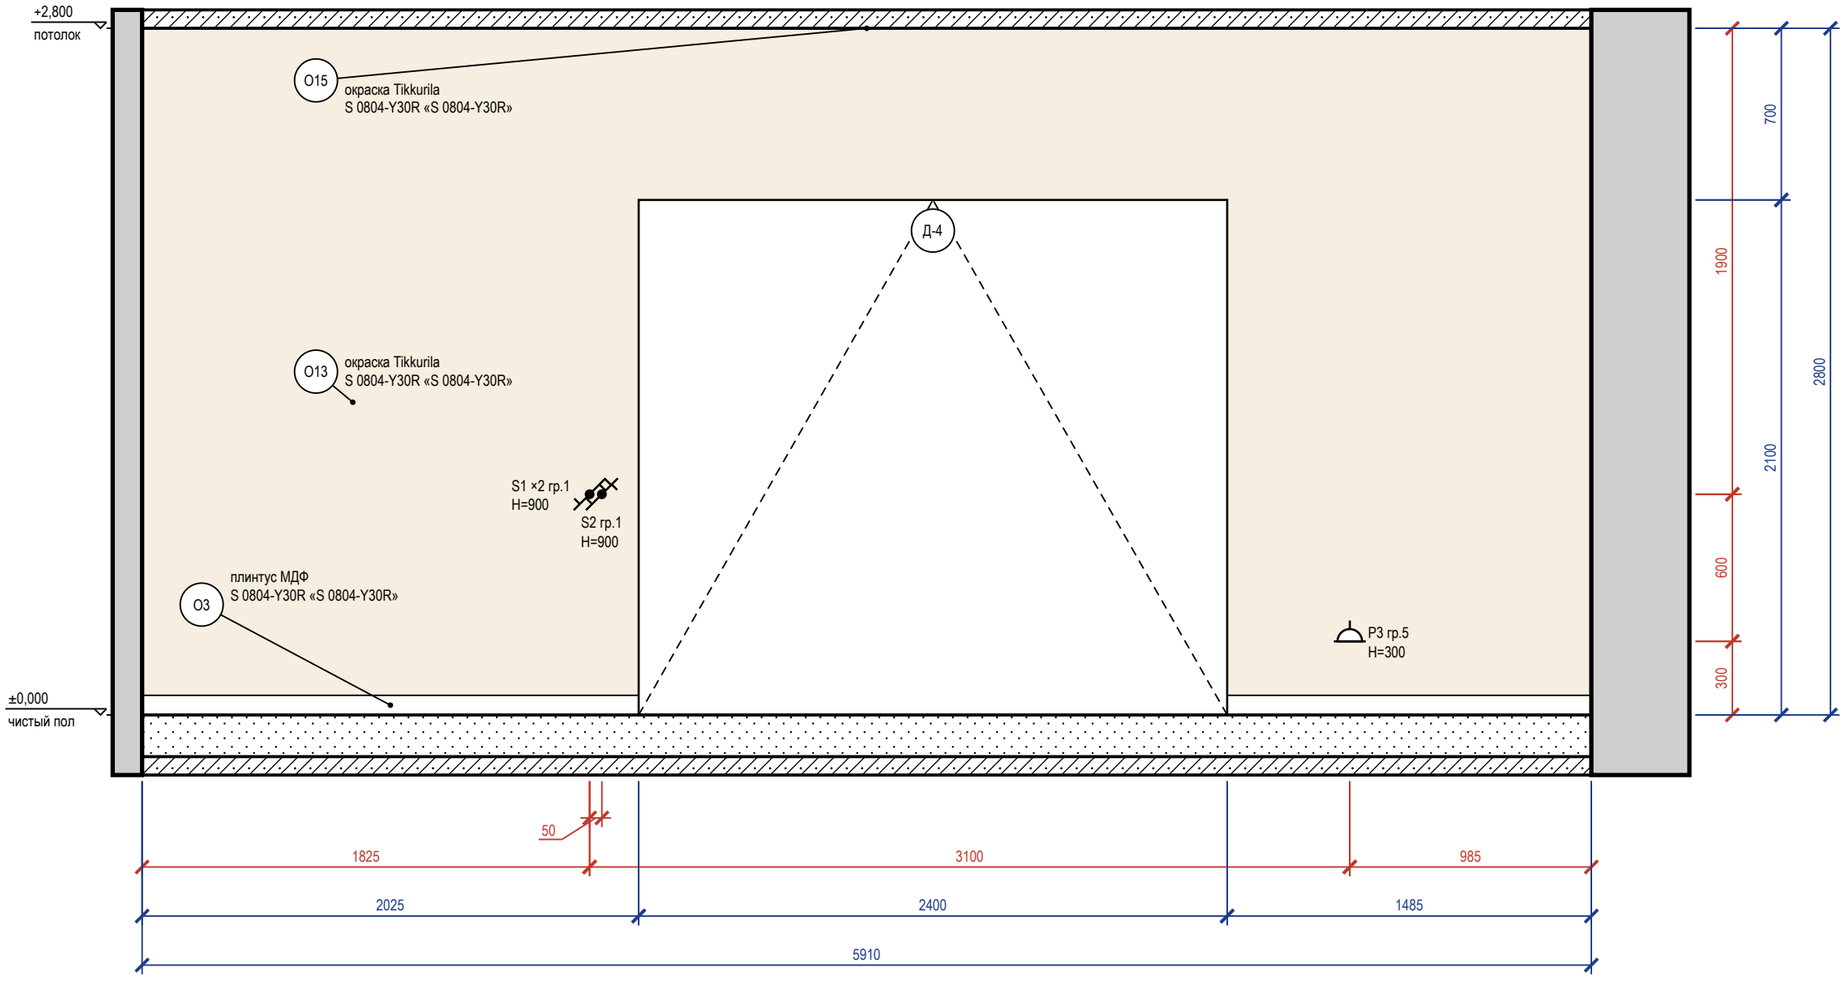


Схема развёрток (М 1:100)

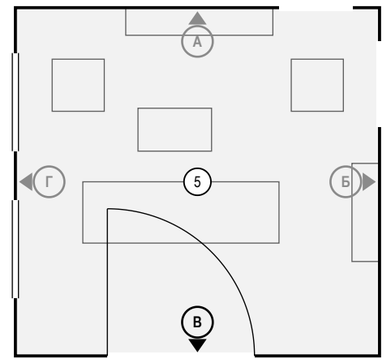

Ведомость отделки (на листе)

Марка	Поверхность	Материал, изделие	Цвет, код	Кол.
О3	плинтус	плинтус МДФ, h 80 мм, аналог: плинтус МДФ под окраску 80×16 мм, полуглянцевая	NCS S 0804-Y30R «S 0804-Y30R»	3,5 м
О13	стены	окраска, Tikkurila Optiva 5 Matt, матовая, подготовка К3	NCS S 0804-Y30R «S 0804-Y30R»	11,5 м²
О15	потолок	окраска, Tikkurila Anti-Reflex 2, глубокоматовая, подготовка Q3	NCS S 0804-Y30R «S 0804-Y30R»	33,7 м²

Визуализация этой стены — лист 72



Примечания

1. Размеры — в мм от чистовых поверхностей стен; условные обозначения и общие указания — лист 2.

					Проект: Дом 331 м²
	Лист	№ док.	Подпись	Дата	Развёртка стены В. Гостиная (пом. 5)
Дизайнер	Кырлан А.С.			19.10.26	

Стадия	Лист	Листов
П	76	155

выпуск 18.10.2026 № ffc1f29499 · стр. 76 из 155

Развёртка стены Г


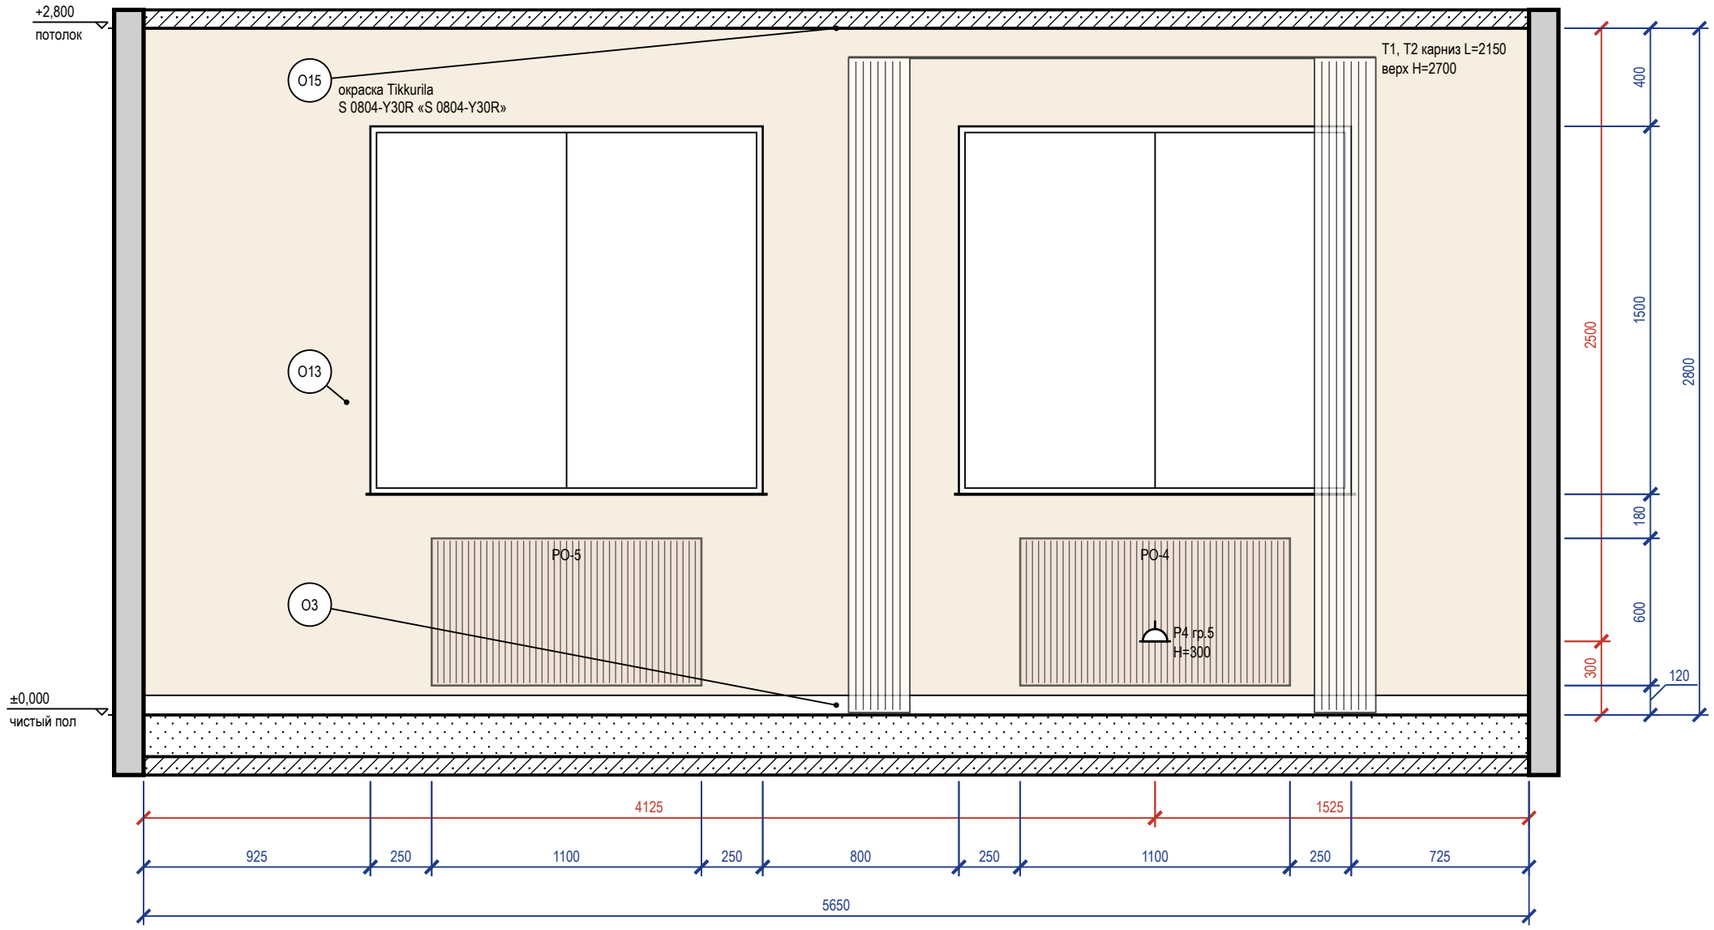


Схема развёрток (М 1:100)

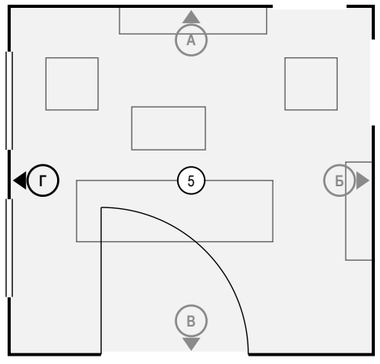

Ведомость отделки (на листе)

Марка	Поверхность	Материал, изделие	Цвет, код	Кол.
О3	плинтус	плинтус МДФ, h 80 мм, аналог: плинтус МДФ под окраску 80×16 мм, полуглянцевая	NCS S 0804-Y30R «S 0804-Y30R»	5,7 м
О13	стены	окраска, Tikkurila Optiva 5 Matt, матовая, подготовка К3	NCS S 0804-Y30R «S 0804-Y30R»	11 м²
О15	потолок	окраска, Tikkurila Anti-Reflex 2, глубокоматовая, подготовка Q3	NCS S 0804-Y30R «S 0804-Y30R»	33,7 м²

Визуализация этой стены — лист 73



Примечания

1. Размеры — в мм от чистовых поверхностей стен; условные обозначения и общие указания — лист 2.
2. Карнизы (шины) — по ведомости текстиля декоратора; длина L и верх Н — по развёртке, крепление — до окраски потолка.

					Проект: Дом 331 м²
	Лист	№ док.	Подпись	Дата	Развёртка стены Г. Гостиная (пом. 5)
Дизайнер	Кырлан А.С.			19.10.26	

Стадия	Лист	Листов
П	77	155

выпуск 18.10.2026 № ffc1f29499 · стр. 77 из 155



					Проект: Дом 331 м²
	Лист	№ док.	Подпись	Дата	
Дизайнер	Кырлан А.С.			19.10.26	Визуализация: Холл с лестницей

Стадия	Лист	Листов
П	78	155

выпуск 18.10.2026 № ffc1f29499 · стр. 78 из 155

Развёртка стены А


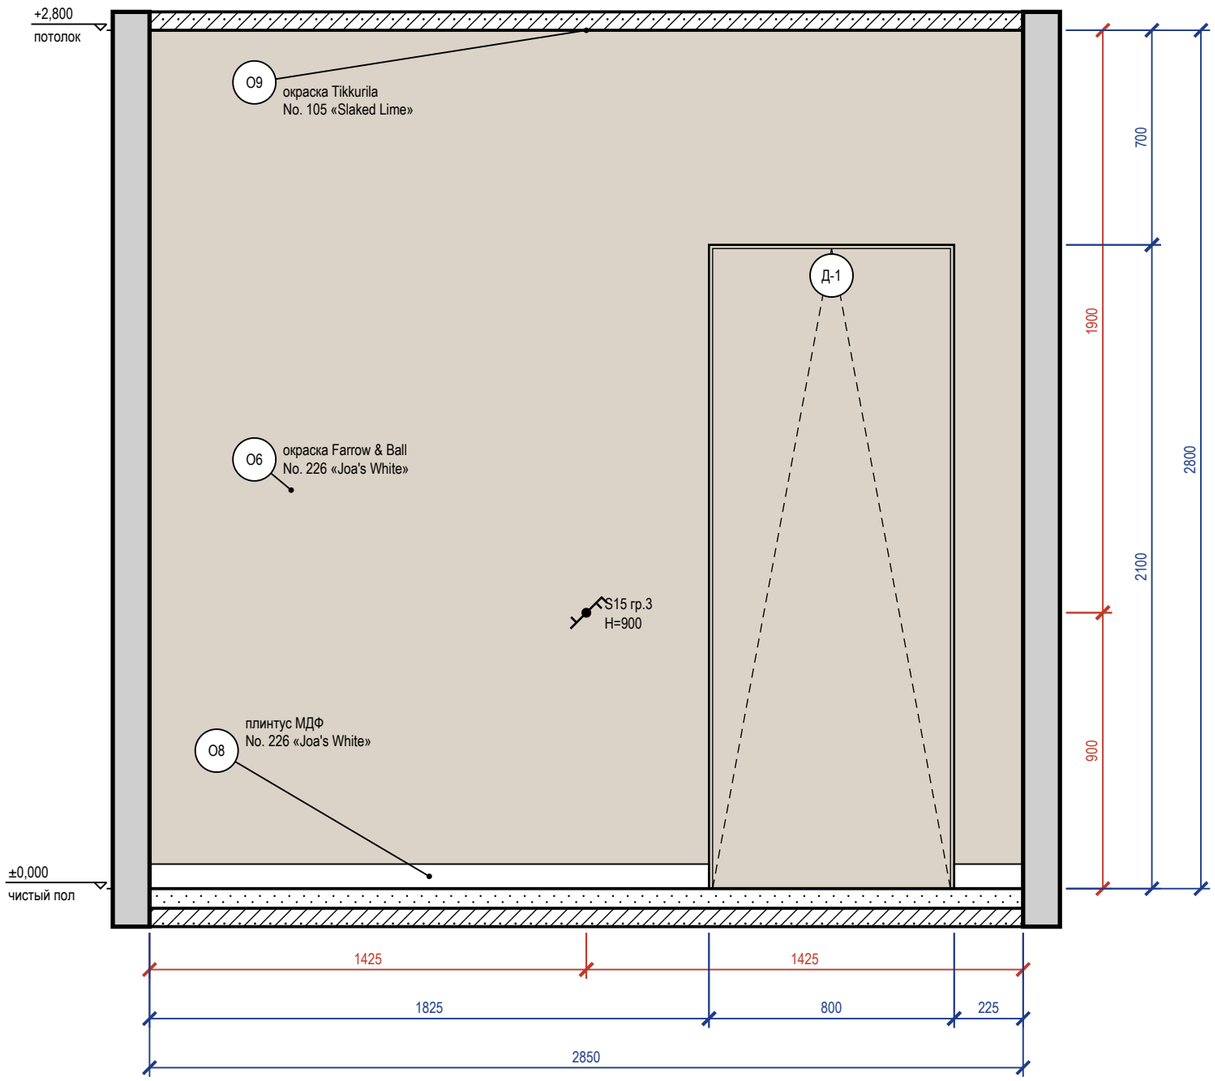


Схема развёрток (М 1:100)

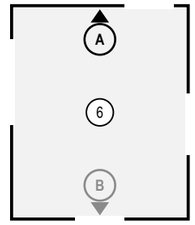


Ведомость отделки (на листе)

Марка	Поверхность	Материал, изделие	Цвет, код	Кол.
О6	стены	окраска, Farrow & Ball Modern Emulsion, матовая, подготовка Q3	Farrow & Ball No. 226 «Joa's White»	6,3 м²
О8	плинтус	плинтус МДФ, h 80 мм, аналог: плинтус МДФ под покраску 80×16	Farrow & Ball No. 226 «Joa's White»	2 м
О9	потолок	окраска, Tikkurila Anti-Reflex 2, глубокоматовая, подготовка Q3	Little Greene No. 105 «Slaked Lime»	10 м²

3 **Дверь скрытого монтажа в плоскости стены, плинтус (М 1:10)**

Узел 3 — лист С3

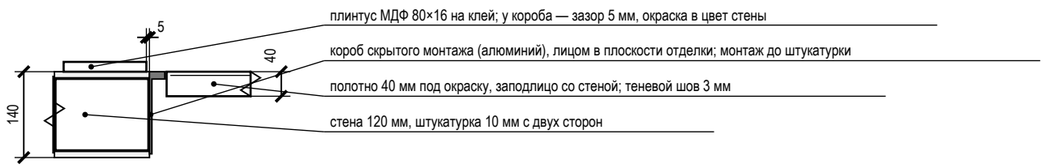

Примечания

1. Размеры — в мм от чистовых поверхностей стен; условные обозначения и общие указания — лист 2.
2. Двери скрытого монтажа — полотно в плоскости стены, отделка стены по полотну, плинтус прерывается у короба (узел — на листе узлов).

					Проект: Дом 331 м²
	Лист	№ док.	Подпись	Дата	Развёртка стены А. Холл с лестницей (пом. 6)
Дизайнер	Кырлан А.С.			19.10.26	

Стадия	Лист	Листов
П	79	155

выпуск 18.10.2026 № ffc1f29499 · стр. 79 из 155

Развёртка стены В


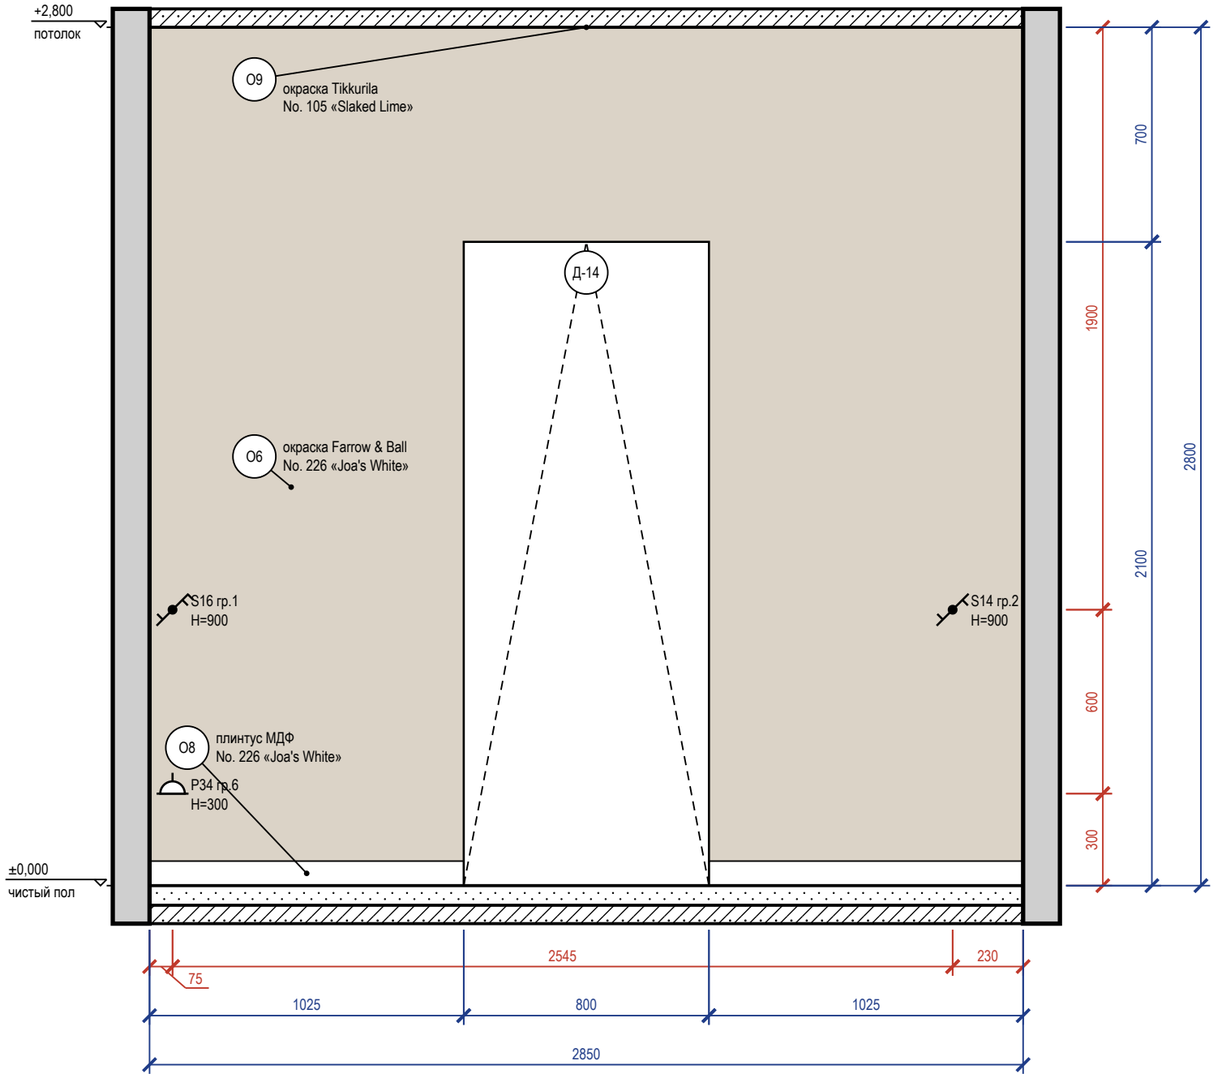


Схема развёрток (М 1:100)

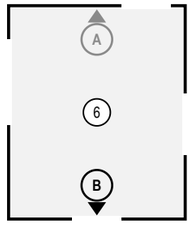

Ведомость отделки (на листе)

Марка	Поверхность	Материал, изделие	Цвет, код	Кол.
О6	стены	окраска, Farrow & Ball Modern Emulsion, матовая, подготовка Q3	Farrow & Ball No. 226 «Joa's White»	6,3 м²
О8	плинтус	плинтус МДФ, h 80 мм, аналог: плинтус МДФ под покраску 80×16	Farrow & Ball No. 226 «Joa's White»	2 м
О9	потолок	окраска, Tikkurila Anti-Reflex 2, глубокоматовая, подготовка Q3	Little Greene No. 105 «Slaked Lime»	10 м²

Визуализация этой стены — лист 78



Примечания

1. Размеры — в мм от чистовых поверхностей стен; условные обозначения и общие указания — лист 2.

					Проект: Дом 331 м²
	Лист	№ док.	Подпись	Дата	Развёртка стены В. Холл с лестницей (пом. 6)
Дизайнер	Кырлан А.С.			19.10.26	

Стадия	Лист	Листов
П	80	155



					Проект: Дом 331 м²
	Лист	№ док.	Подпись	Дата	Визуализация кладовой
Дизайнер	Кырлан А.С.			19.10.26	

Стадия	Лист	Листов
П	81	155

выпуск 18.10.2026 № ffc1f29499 · стр. 81 из 155

Развёртка стены В


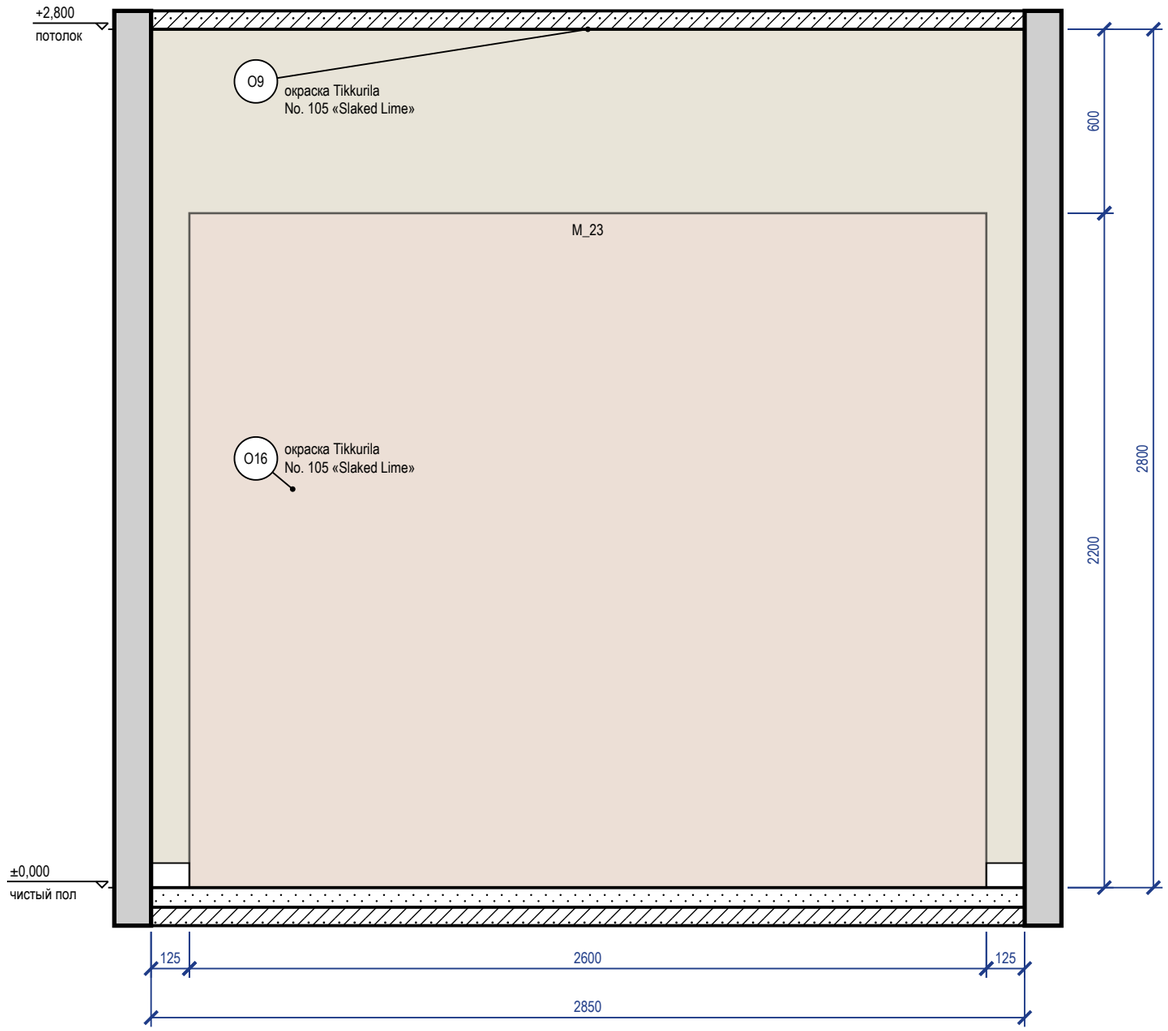



Схема развёрток (М 1:100)

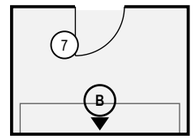

Ведомость отделки (на листе)

Марка	Поверхность	Материал, изделие	Цвет, код	Кол.
O9	потолок	окраска, Tikkurila Anti-Reflex 2, глубокоматовая, подготовка Q3	Little Greene No. 105 «Slaked Lime»	6 м²
O16	стены	окраска, Tikkurila Harmony, матовая, подготовка Q3	Little Greene No. 105 «Slaked Lime»	8 м²
O17	плинтус	плинтус МДФ, h 80 мм, аналог: плинтус МДФ под покраску 80×16	Little Greene No. 105 «Slaked Lime»	0,3 м

Визуализация этой стены — лист 81

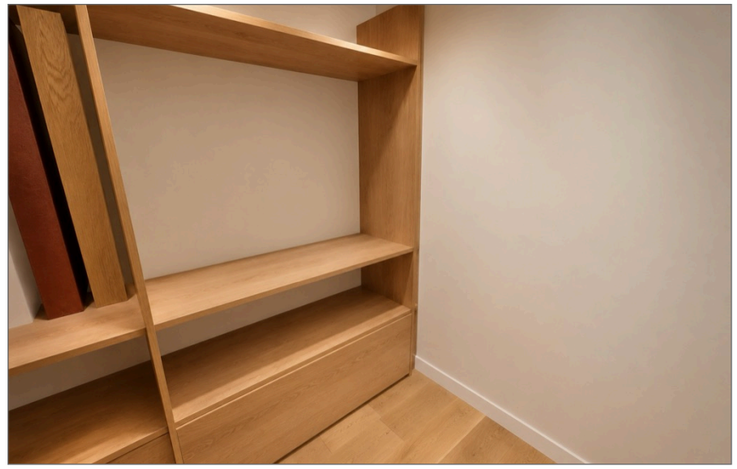

Примечания

1. Размеры — в мм от чистовых поверхностей стен; условные обозначения и общие указания — лист 2.

					Проект: Дом 331 м²
	Лист	№ док.	Подпись	Дата	Развёртки стен. Кладовая (пом. 7)
Дизайнер	Кырлан А.С.			19.10.26	

Стадия	Лист	Листов
П	82	155

выпуск 18.10.2026 № ffc1f29499 · стр. 82 из 155



					Проект: Дом 331 м²
	Лист	№ док.	Подпись	Дата	Визуализация прихожей
Дизайнер	Кырлан А.С.			19.10.26	

Стадия	Лист	Листов
П	83	155

выпуск 18.10.2026 № ffc1f29499 · стр. 83 из 155



					Проект: Дом 331 м²
	Лист	№ док.	Подпись	Дата	
Дизайнер	Кырлан А.С.			19.10.26	Визуализация прихожей

Стадия	Лист	Листов
П	84	155

выпуск 18.10.2026 · ffc1f29499 · стр. 84 из 155

Развёртка стены А


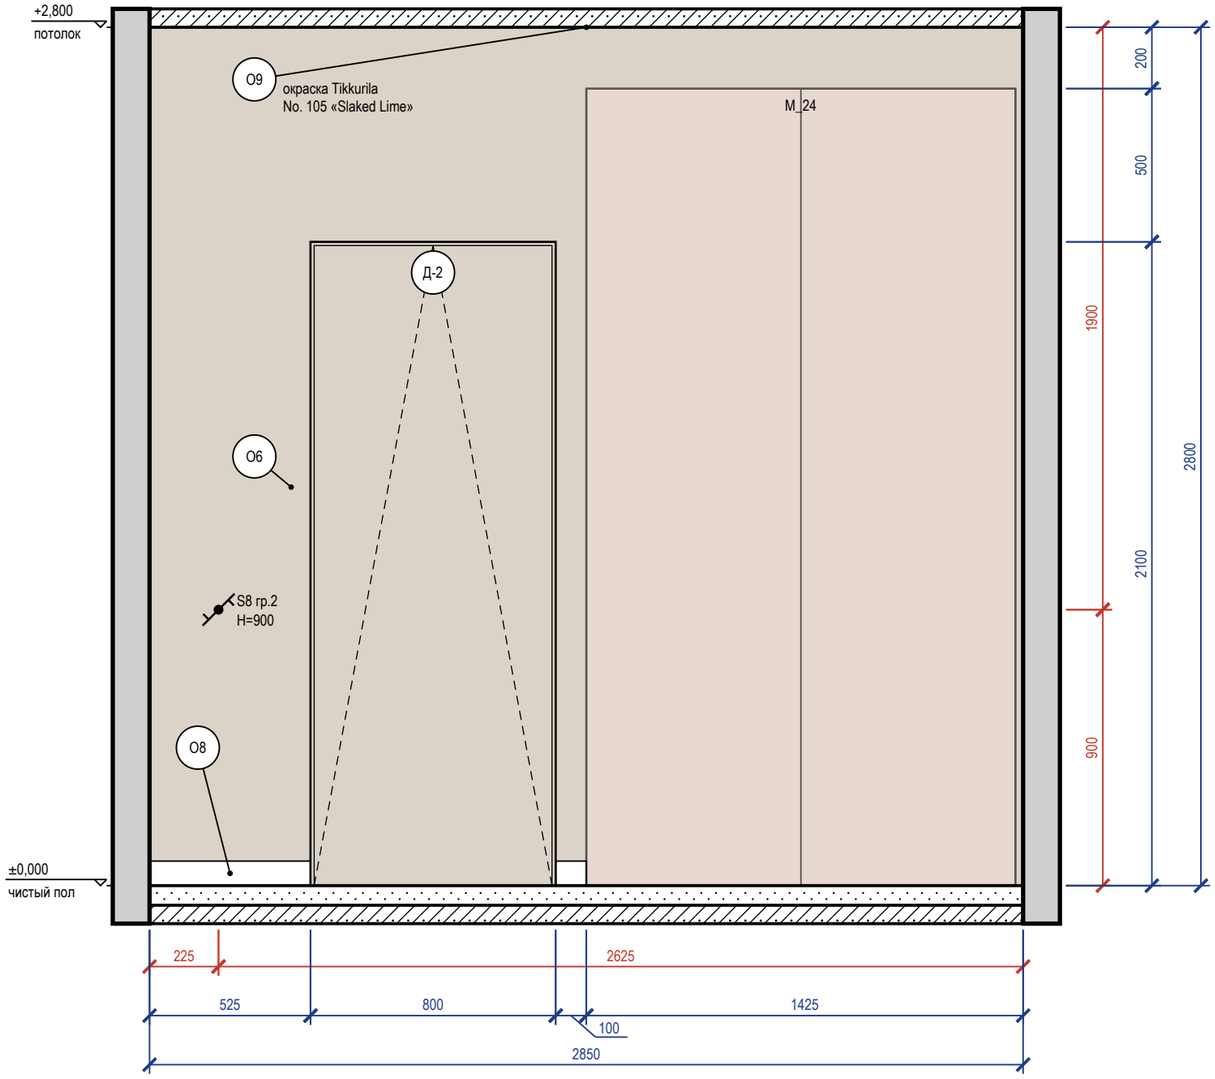


Схема развёрток (М 1:100)

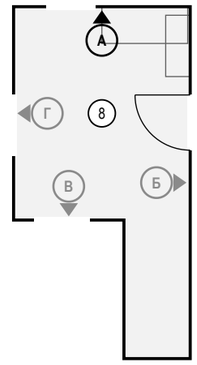

Ведомость отделки (на листе)

Марка	Поверхность	Материал, изделие	Цвет, код	Кол.
О6	стены	окраска, Farrow & Ball Modern Emulsion, матовая, подготовка Q3	Farrow & Ball No. 226 «Joa's White»	6,3 м²
О8	плинтус	плинтус МДФ, h 80 мм, аналог: плинтус МДФ под покраску 80×16	Farrow & Ball No. 226 «Joa's White»	0,6 м
О9	потолок	окраска, Tikkurila Anti-Reflex 2, глубокоматовая, подготовка Q3	Little Greene No. 105 «Slaked Lime»	12,5 м²

Визуализация этой стены — лист 83



Примечания

1. Размеры — в мм от чистовых поверхностей стен; условные обозначения и общие указания — лист 2.
2. Двери скрытого монтажа — полотно в плоскости стены, отделка стены по полотну, плинтус прерывается у короба (узел — на листе узлов).

	Лист	№ док.	Подпись	Дата
Дизайнер	Кырлан А.С.			19.10.26

Проект: Дом 331 м²

Развёртка стены А. Прихожая (пом. 8)

Стадия	Лист	Листов
П	85	155

выпуск 18.10.2026 № ffc1f29499 · стр. 85 из 155

Развёртка стены Б


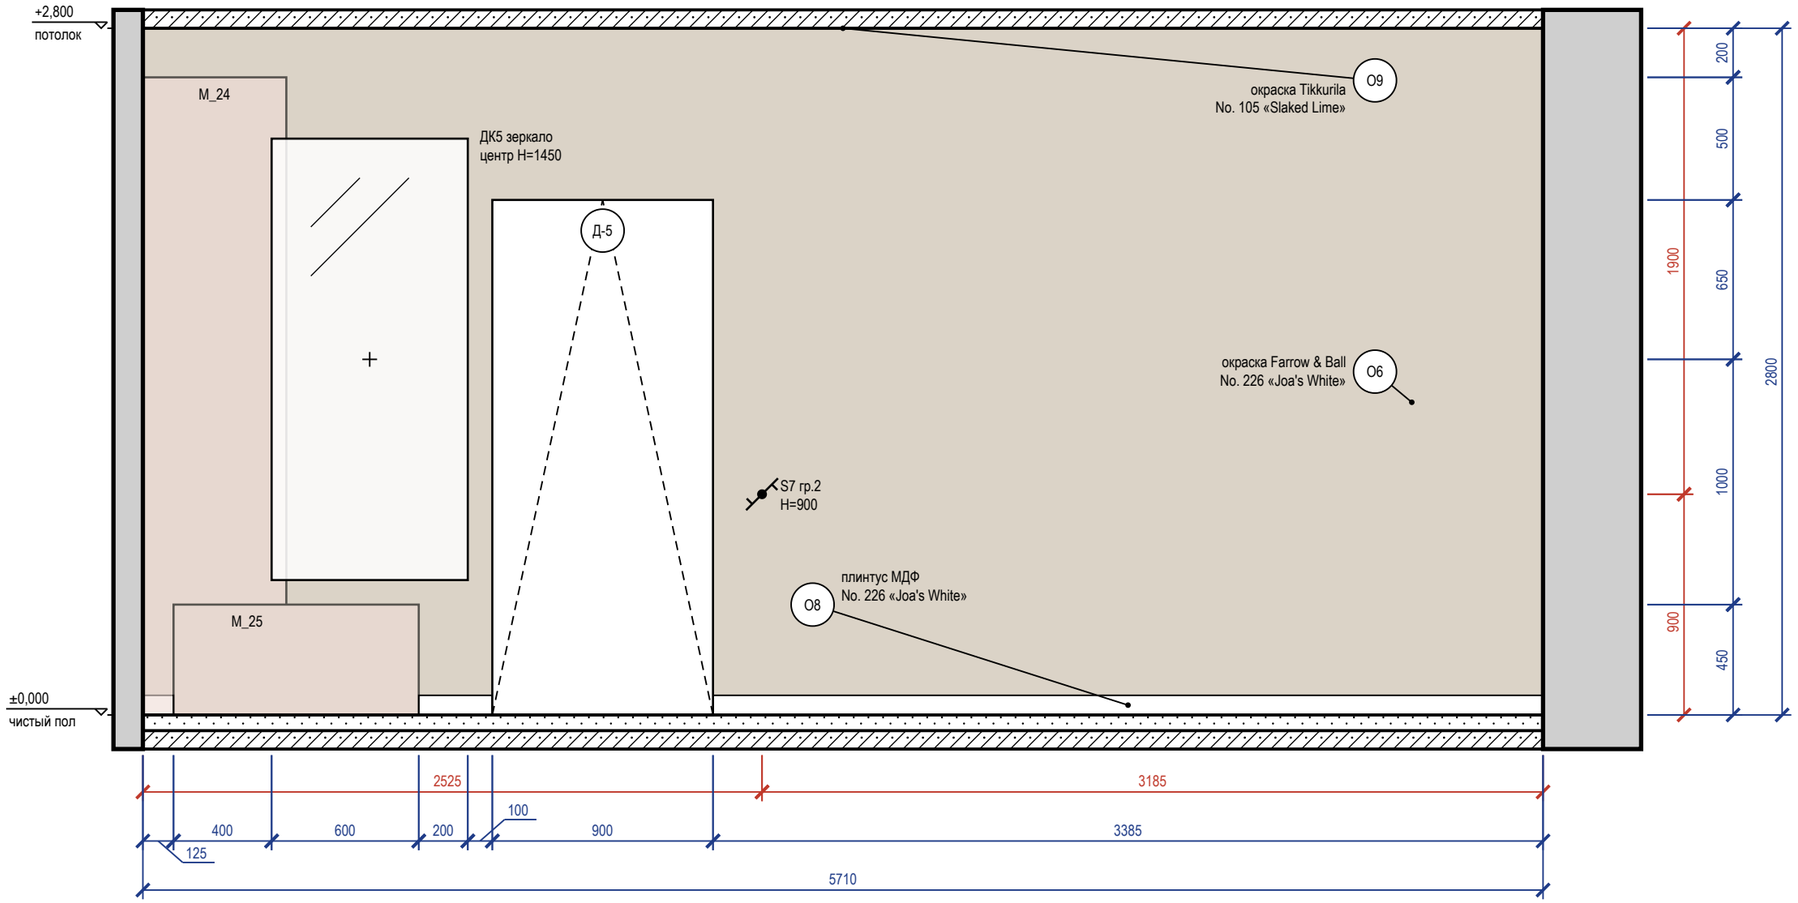


Схема развёрток (М 1:100)

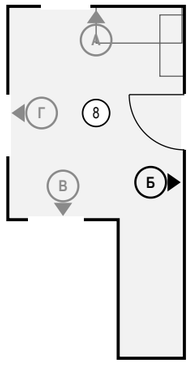

Ведомость отделки (на листе)

Марка	Поверхность	Материал, изделие	Цвет, код	Кол.
O6	стены	окраска, Farrow & Ball Modern Emulsion, матовая, подготовка Q3	Farrow & Ball No. 226 «Joa's White»	14,1 м²
O8	плинтус	плинтус МДФ, h 80 мм, аналог: плинтус МДФ под покраску 80×16	Farrow & Ball No. 226 «Joa's White»	3,8 м
O9	потолок	окраска, Tikkurila Anti-Reflex 2, глубокоматовая, подготовка Q3	Little Greene No. 105 «Slaked Lime»	12,5 м²

Визуализация этой стены — лист 84



Примечания

1. Размеры — в мм от чистовых поверхностей стен; условные обозначения и общие указания — лист 2.
2. Картины и зеркала крепить к основанию по паспорту изделия (закладные и анкеры — в перечне скрытых работ); крест — ось центра предмета.

					Проект: Дом 331 м²		
	Лист	№ док.	Подпись	Дата	Развёртка стены Б. Прихожая (пом. 8)	Стадия	Лист	Листов
Дизайнер	Кырлан А.С.			19.10.26		П	86	155

выпуск 18.10.2026 № ffc1f29499 · стр. 86 из 155

Развёртка стены В


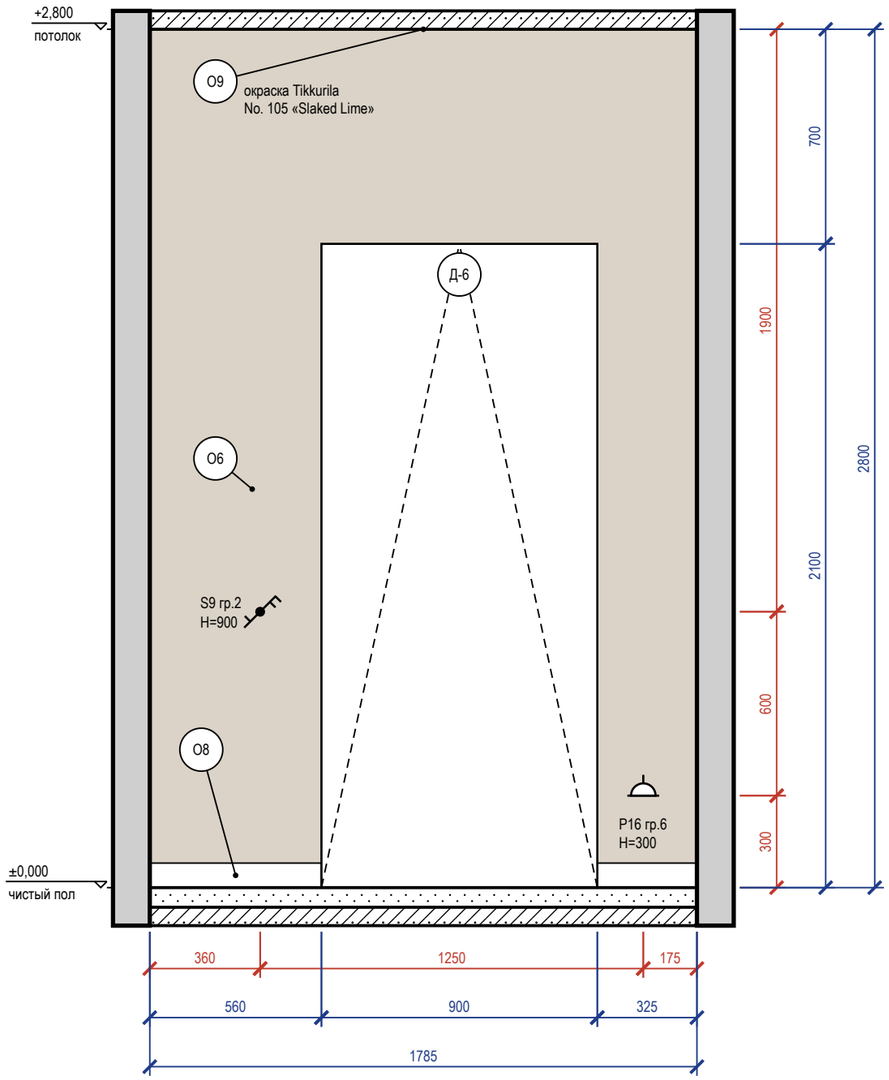


Схема развёрток (М 1:100)

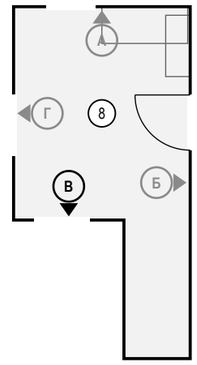

Ведомость отделки (на листе)

Марка	Поверхность	Материал, изделие	Цвет, код	Кол.
О6	стены	окраска, Farrow & Ball Modern Emulsion, матовая, подготовка Q3	Farrow & Ball No. 226 «Joa's White»	3,1 м²
О8	плинтус	плинтус МДФ, h 80 мм, аналог: плинтус МДФ под покраску 80×16	Farrow & Ball No. 226 «Joa's White»	0,9 м
О9	потолок	окраска, Tikkurila Anti-Reflex 2, глубокоматовая, подготовка Q3	Little Greene No. 105 «Slaked Lime»	12,5 м²

Примечания

1. Размеры — в мм от чистовых поверхностей стен; условные обозначения и общие указания — лист 2.

					Проект: Дом 331 м²
	Лист	№ док.	Подпись	Дата	Развёртка стены В. Прихожая (пом. 8)
Дизайнер	Кырлан А.С.			19.10.26	

Стадия	Лист	Листов
П	87	155

выпуск 18.10.2026 · ffc1f29499 · стр. 87 из 155

Развёртка стены Г


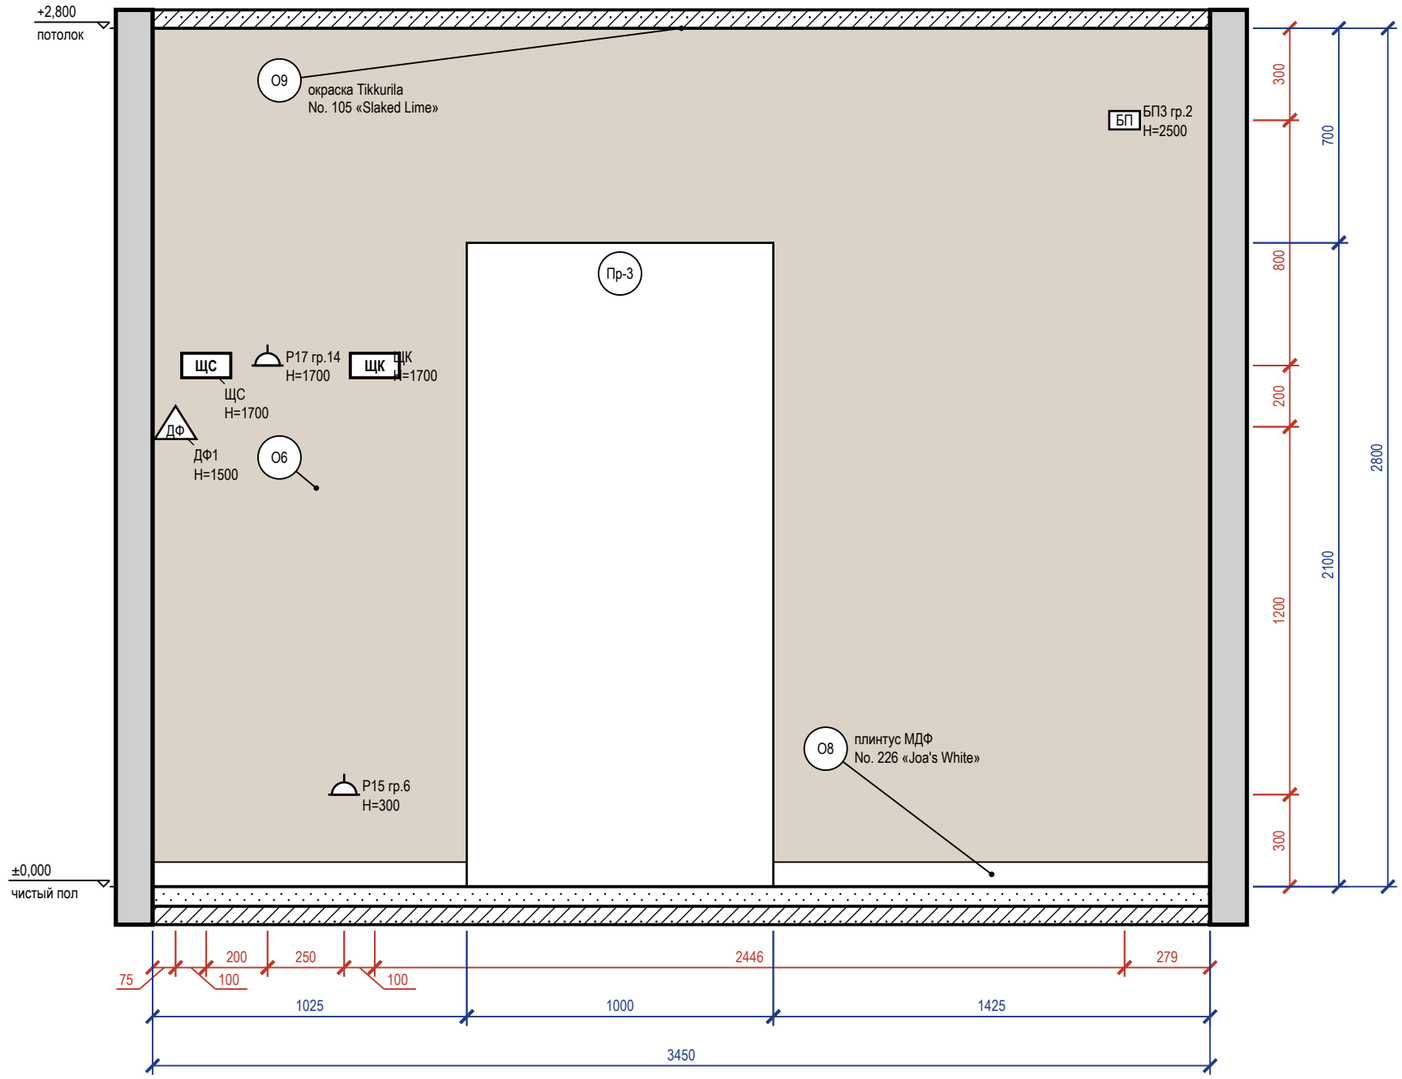


Схема развёрток (М 1:100)

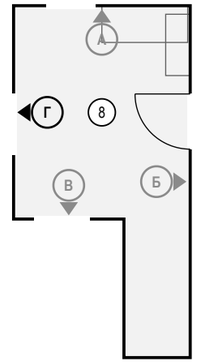

Ведомость отделки (на листе)

Марка	Поверхность	Материал, изделие	Цвет, код	Кол.
О6	стены	окраска, Farrow & Ball Modern Emulsion, матовая, подготовка Q3	Farrow & Ball No. 226 «Joa's White»	7,6 м²
О8	плинтус	плинтус МДФ, h 80 мм, аналог: плинтус МДФ под покраску 80×16	Farrow & Ball No. 226 «Joa's White»	2,5 м
О9	потолок	окраска, Tikkurila Anti-Reflex 2, глубокоматовая, подготовка Q3	Little Greene No. 105 «Slaked Lime»	12,5 м²

Примечания

1. Размеры — в мм от чистовых поверхностей стен; условные обозначения и общие указания — лист 2.

	Лист	№ док.	Подпись	Дата
Дизайнер	Кырлан А.С.			19.10.26

Проект: Дом 331 м²

Развёртка стены Г. Прихожая (пом. 8)

Стадия	Лист	Листов
П	88	155

выпуск 18.10.2026 № ffc1f29499 · стр. 88 из 155

Развёртка стены Г


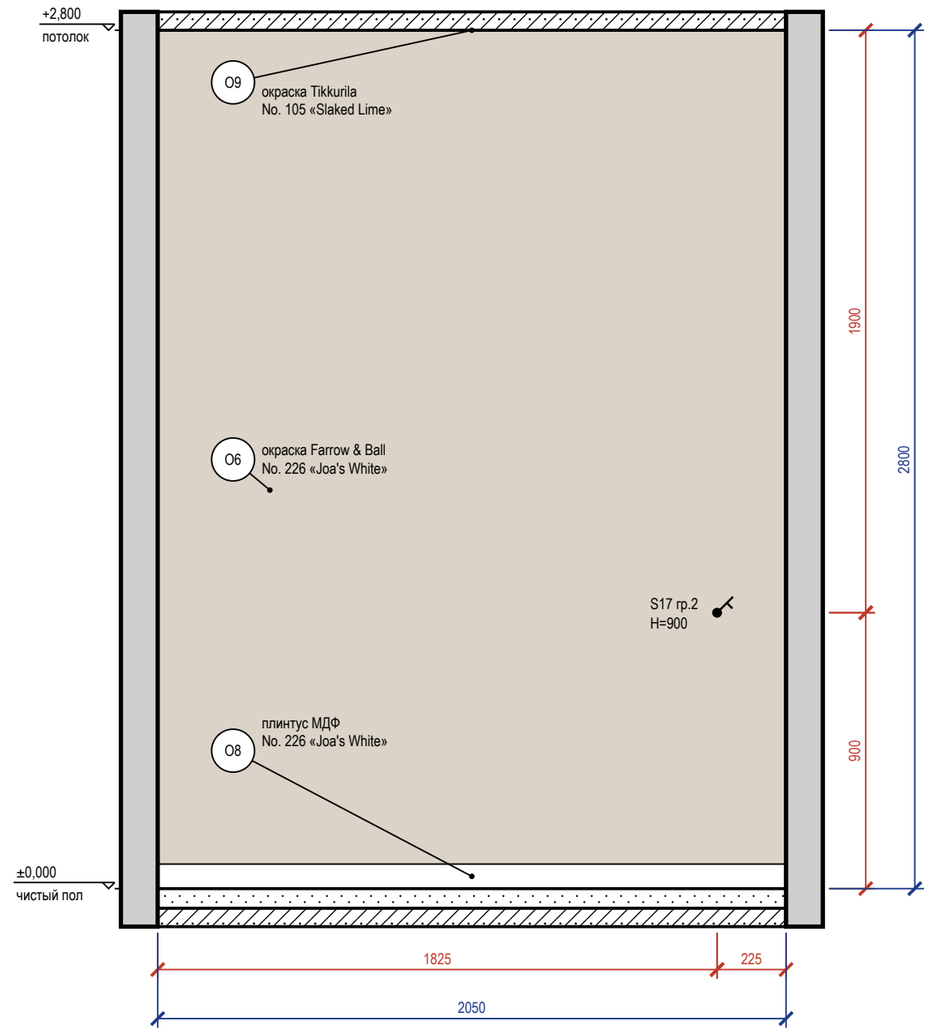


Схема развёрток (М 1:100)

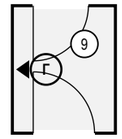

Ведомость отделки (на листе)

Марка	Поверхность	Материал, изделие	Цвет, код	Кол.
О6	стены	окраска, Farrow & Ball Modern Emulsion, матовая, подготовка Q3	Farrow & Ball No. 226 «Joa's White»	5,7 м²
О8	плинтус	плинтус МДФ, h 80 мм, аналог: плинтус МДФ под покраску 80×16	Farrow & Ball No. 226 «Joa's White»	2 м
О9	потолок	окраска, Tikkurila Anti-Reflex 2, глубокоматовая, подготовка Q3	Little Greene No. 105 «Slaked Lime»	3,5 м²

Примечания

1. Размеры — в мм от чистовых поверхностей стен; условные обозначения и общие указания — лист 2.

					Проект: Дом 331 м²
	Лист	№ док.	Подпись	Дата	Развёртки стен. Тамбур (пом. 9)
Дизайнер	Кырлан А.С.			19.10.26	

Стадия	Лист	Листов
П	89	155

выпуск 18.10.2026 № ffc1f29499 · стр. 89 из 155



					Проект: Дом 331 м²
	Лист	№ док.	Подпись	Дата	
Дизайнер	Кырлан А.С.			19.10.26	Визуализация: Гараж

Стадия	Лист	Листов
П	90	155

выпуск 18.10.2026 № ffc1f29499 · стр. 90 из 155

Развёртка стены А


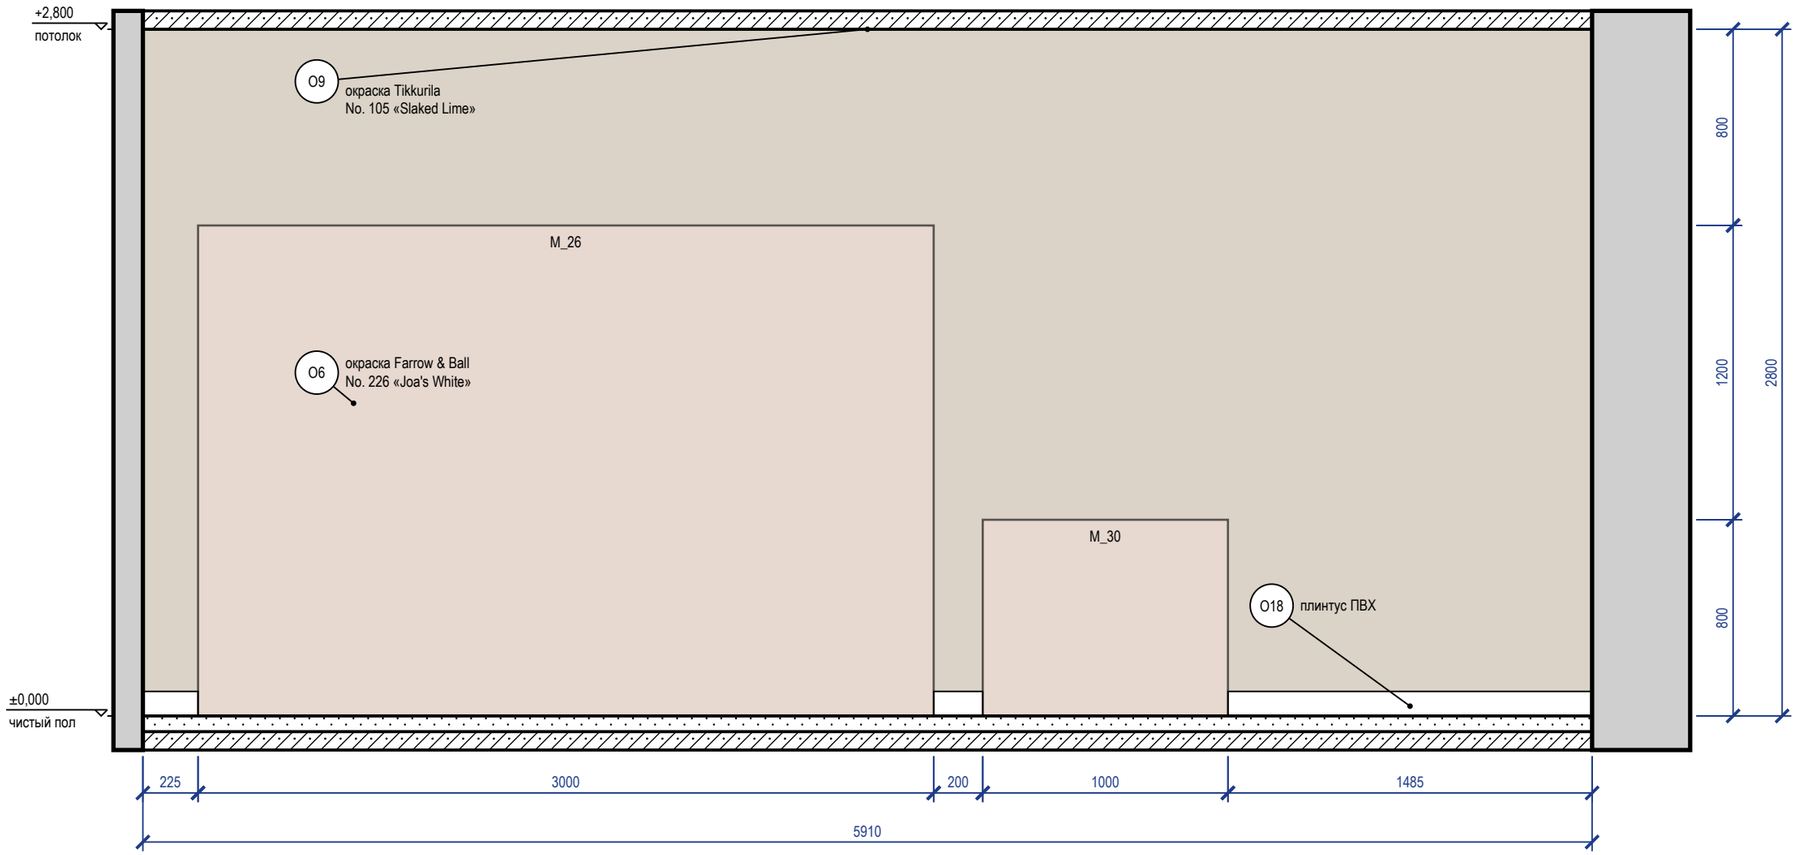


Схема развёрток (М 1:100)

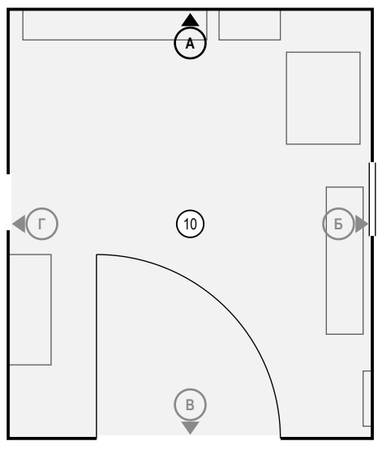

Ведомость отделки (на листе)

Марка	Поверхность	Материал, изделие	Цвет, код	Кол.
О6	стены	окраска, Farrow & Ball Modern Emulsion, матовая, подготовка Q3	Farrow & Ball No. 226 «Joa's White»	16,5 м²
О9	потолок	окраска, Tikkurila Anti-Reflex 2, глубокоматовая, подготовка Q3	Little Greene No. 105 «Slaked Lime»	41,6 м²
О18	плинтус	плинтус ПВХ, h 100 мм, аналог: плинтус ПВХ влагостойкий 100 мм, серый		1,9 м

Визуализация этой стены — лист 90



Примечания

1. Размеры — в мм от чистовых поверхностей стен; условные обозначения и общие указания — лист 2.

					Проект: Дом 331 м²
	Лист	№ док.	Подпись	Дата	Развёртка стены А. Гараж (пом. 10)
Дизайнер	Кырлан А.С.			19.10.26	

Стадия	Лист	Листов
П	91	155

выпуск 18.10.2026 № ffc1f29499 · стр. 91 из 155

Развёртка стены Б


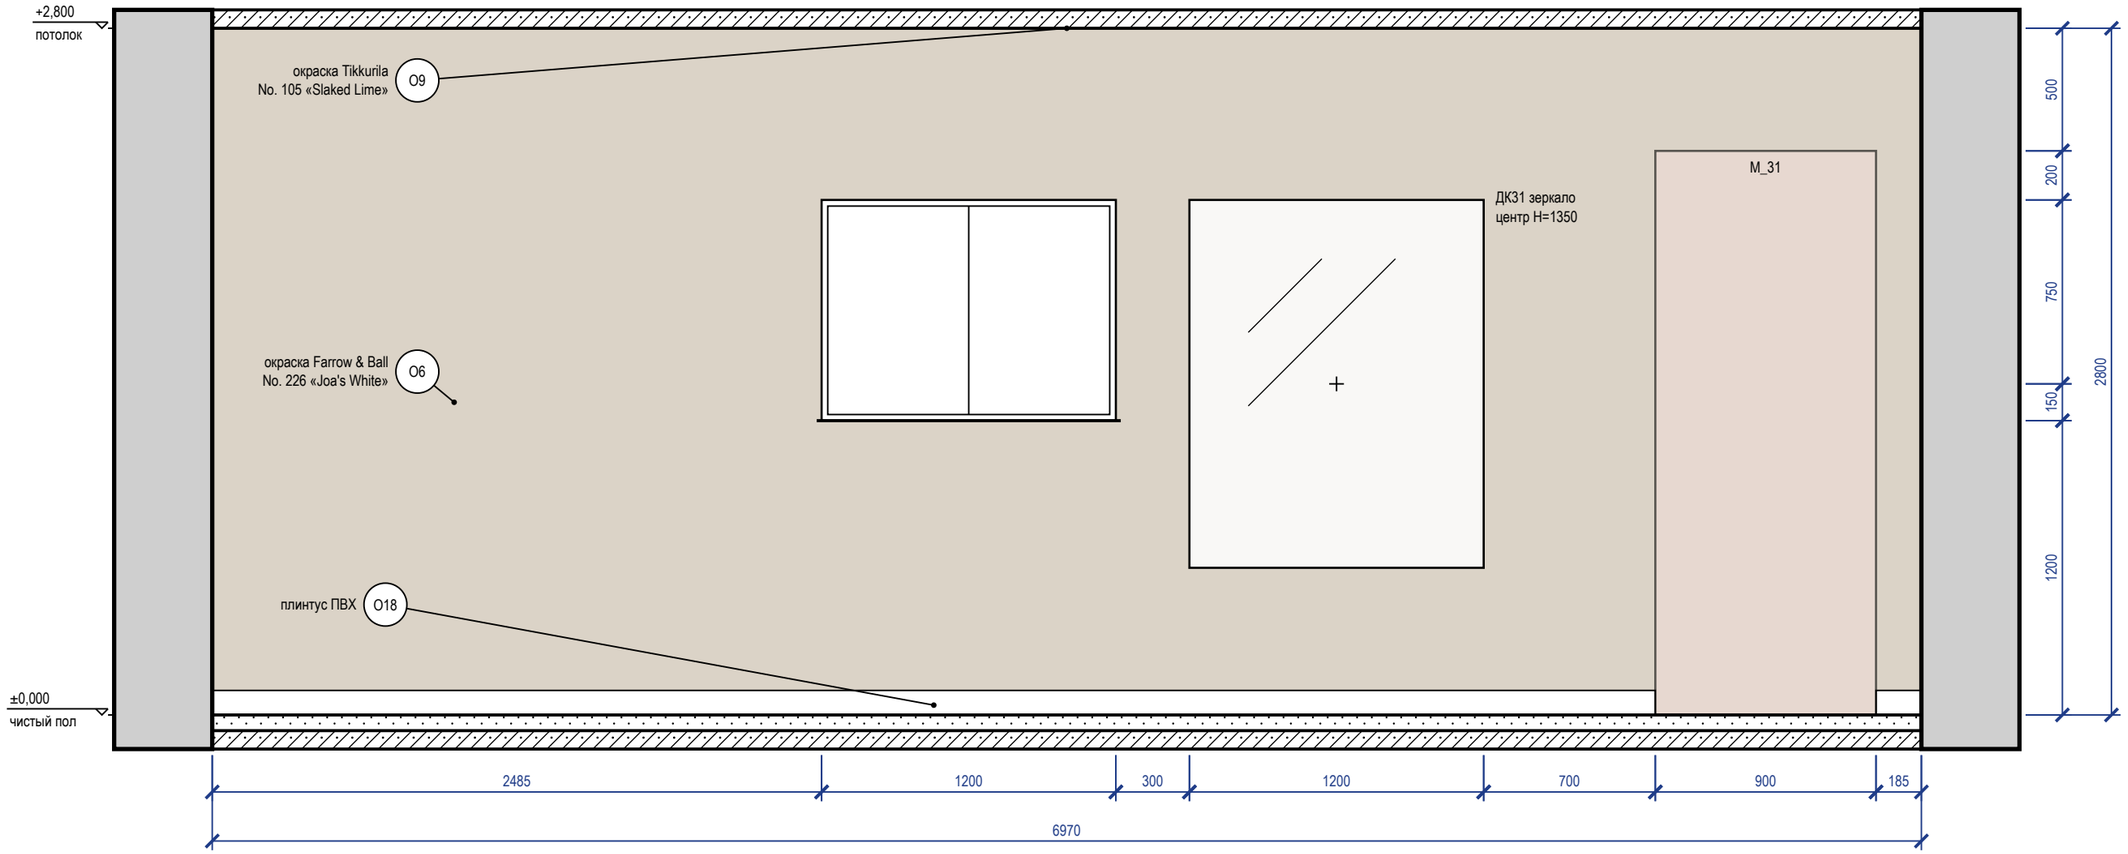


Схема развёрток (М 1:100)

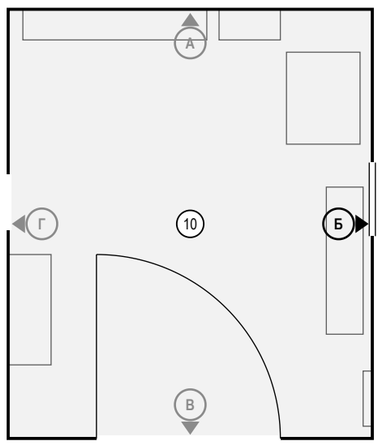

Ведомость отделки (на листе)

Марка	Поверхность	Материал, изделие	Цвет, код	Кол.
О6	стены	окраска, Farrow & Ball Modern Emulsion, матовая, подготовка Q3	Farrow & Ball No. 226 «Joa's White»	18,4 м²
О9	потолок	окраска, Tikkurila Anti-Reflex 2, глубокоматовая, подготовка Q3	Little Greene No. 105 «Slaked Lime»	41,6 м²
О18	плинтус	плинтус ПВХ, h 100 мм, аналог: плинтус ПВХ влагостойкий 100 мм, серый		6,1 м

Примечания

1. Размеры — в мм от чистовых поверхностей стен; условные обозначения и общие указания — лист 2.
2. Картины и зеркала крепить к основанию по паспорту изделия (закладные и анкеры — в перечне скрытых работ); крест — ось центра предмета.

					Проект: Дом 331 м²
	Лист	№ док.	Подпись	Дата	
Дизайнер	Кырлан А.С.			19.10.26	Развёртка стены Б. Гараж (пом. 10)

Стадия	Лист	Листов
П	92	155

выпуск 18.10.2026 № ffc1f29499 · стр. 92 из 155

Развёртка стены В


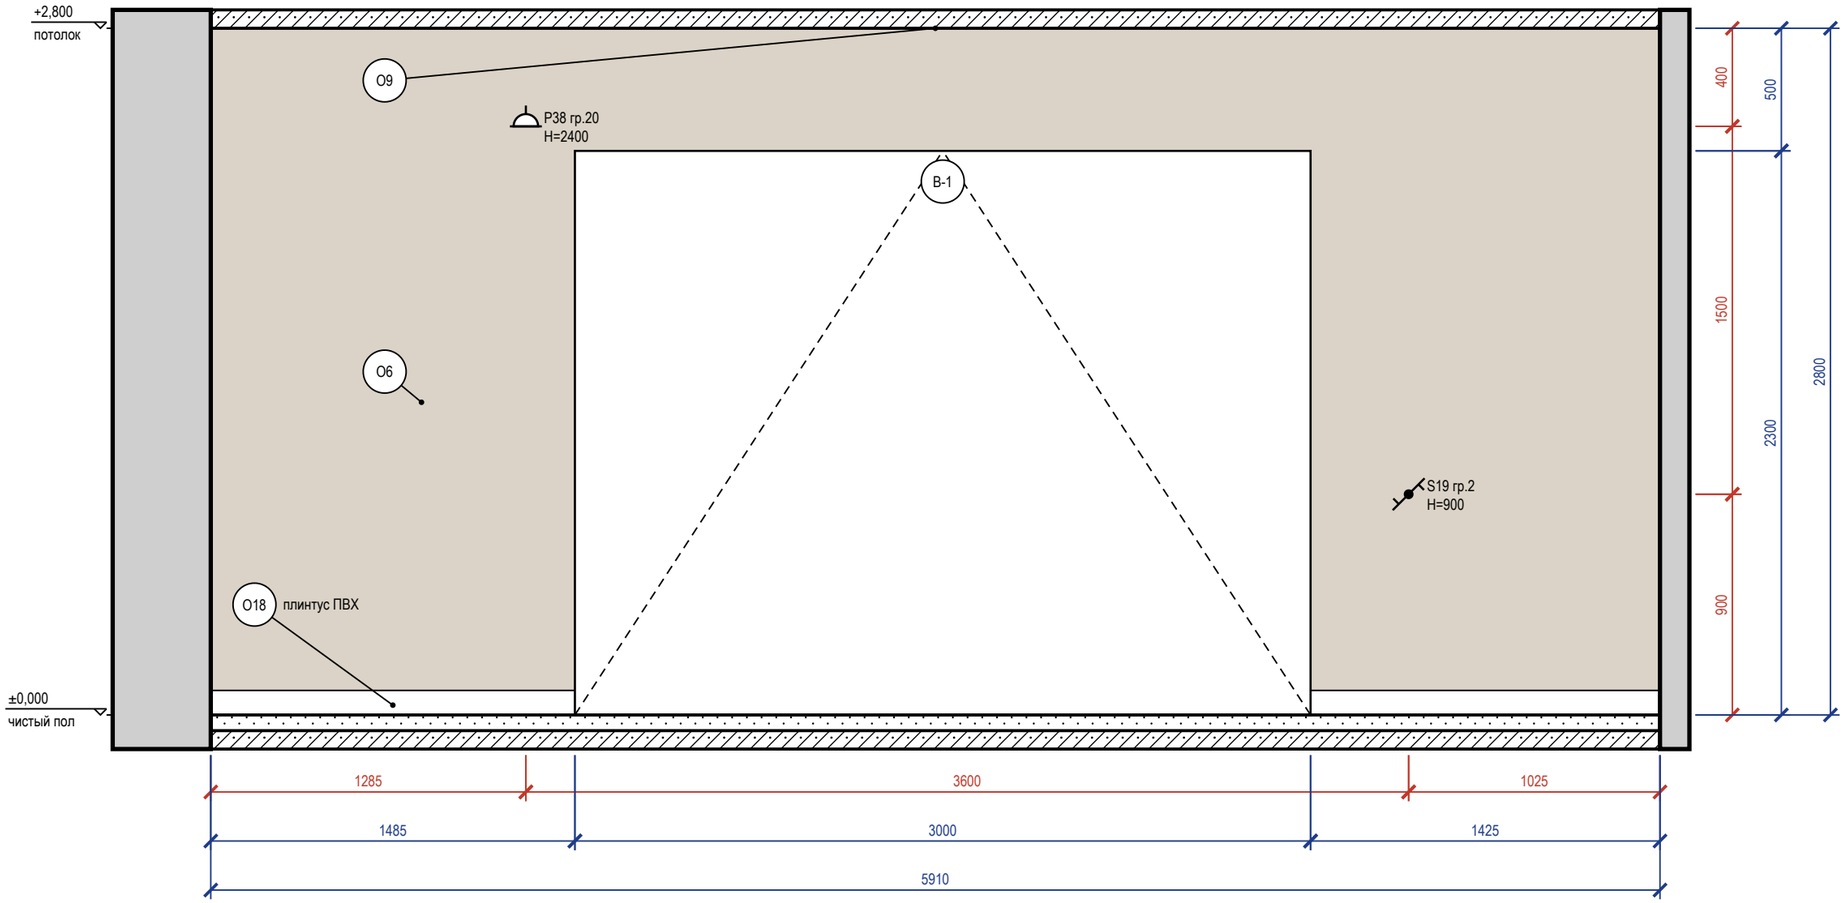


Схема развёрток (М 1:100)

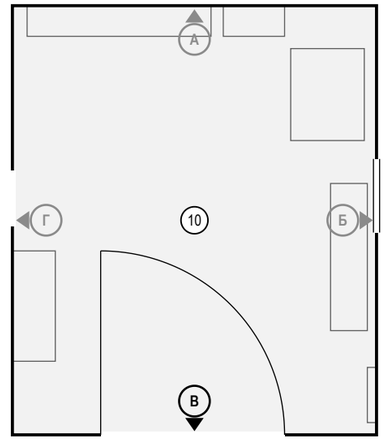

Ведомость отделки (на листе)

Марка	Поверхность	Материал, изделие	Цвет, код	Кол.
О6	стены	окраска, Farrow & Ball Modern Emulsion, матовая, подготовка Q3	Farrow & Ball No. 226 «Joa's White»	9,6 м²
О9	потолок	окраска, Tikkurila Anti-Reflex 2, глубокоматовая, подготовка Q3	Little Greene No. 105 «Slaked Lime»	41,6 м²
О18	плинтус	плинтус ПВХ, h 100 мм, аналог: плинтус ПВХ влагостойкий 100 мм, серый		2,9 м

Примечания

1. Размеры — в мм от чистовых поверхностей стен; условные обозначения и общие указания — лист 2.

					Проект: Дом 331 м²
	Лист	№ док.	Подпись	Дата	Развёртка стены В. Гараж (пом. 10)
Дизайнер	Кырлан А.С.			19.10.26	

Стадия	Лист	Листов
П	93	155

выпуск 18.10.2026 № ffc1f29499 · стр. 93 из 155

Развёртка стены Г


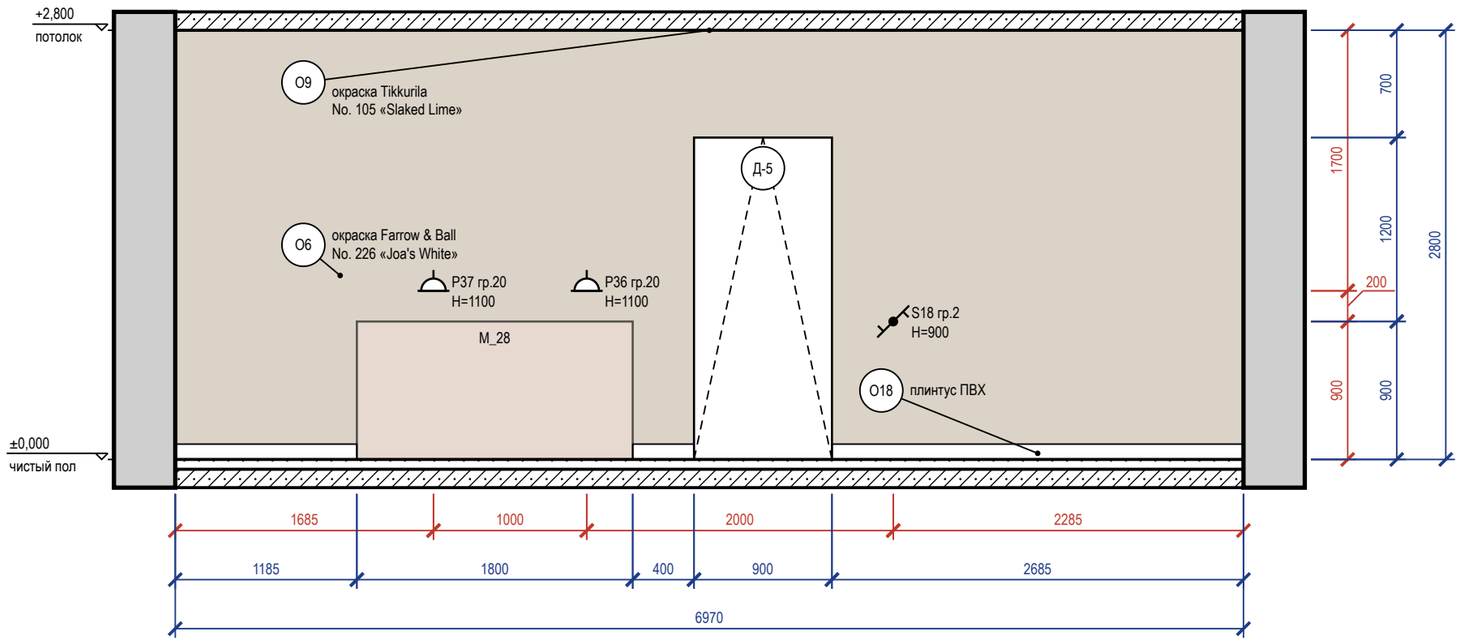


Схема развёрток (М 1:100)

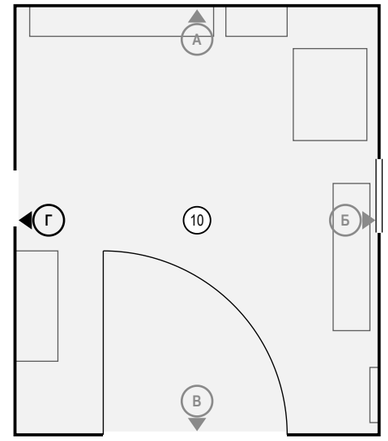

Ведомость отделки (на листе)

Марка	Поверхность	Материал, изделие	Цвет, код	Кол.
О6	стены	окраска, Farrow & Ball Modern Emulsion, матовая, подготовка Q3	Farrow & Ball No. 226 «Joa's White»	17,6 м²
О9	потолок	окраска, Tikkurila Anti-Reflex 2, глубокоматовая, подготовка Q3	Little Greene No. 105 «Slaked Lime»	41,6 м²
О18	плинтус	плинтус ПВХ, h 100 мм, аналог: плинтус ПВХ влагостойкий 100 мм, серый		4,3 м

Примечания

1. Размеры — в мм от чистовых поверхностей стен; условные обозначения и общие указания — лист 2.

	Лист	№ док.	Подпись	Дата
Дизайнер	Кырлан А.С.			19.10.26

Проект: Дом 331 м²

Развёртка стены Г. Гараж (пом. 10)

Стадия	Лист	Листов
П	94	155

выпуск 18.10.2026 № ffc1f29499 · стр. 94 из 155



					Проект: Дом 331 м²
	Лист	№ док.	Подпись	Дата	
Дизайнер	Кырлан А.С.			19.10.26	Визуализация: Веранда

Стадия	Лист	Листов
П	95	155

выпуск 18.10.2026 № ffc1f29499 · стр. 95 из 155

Развёртка стены А


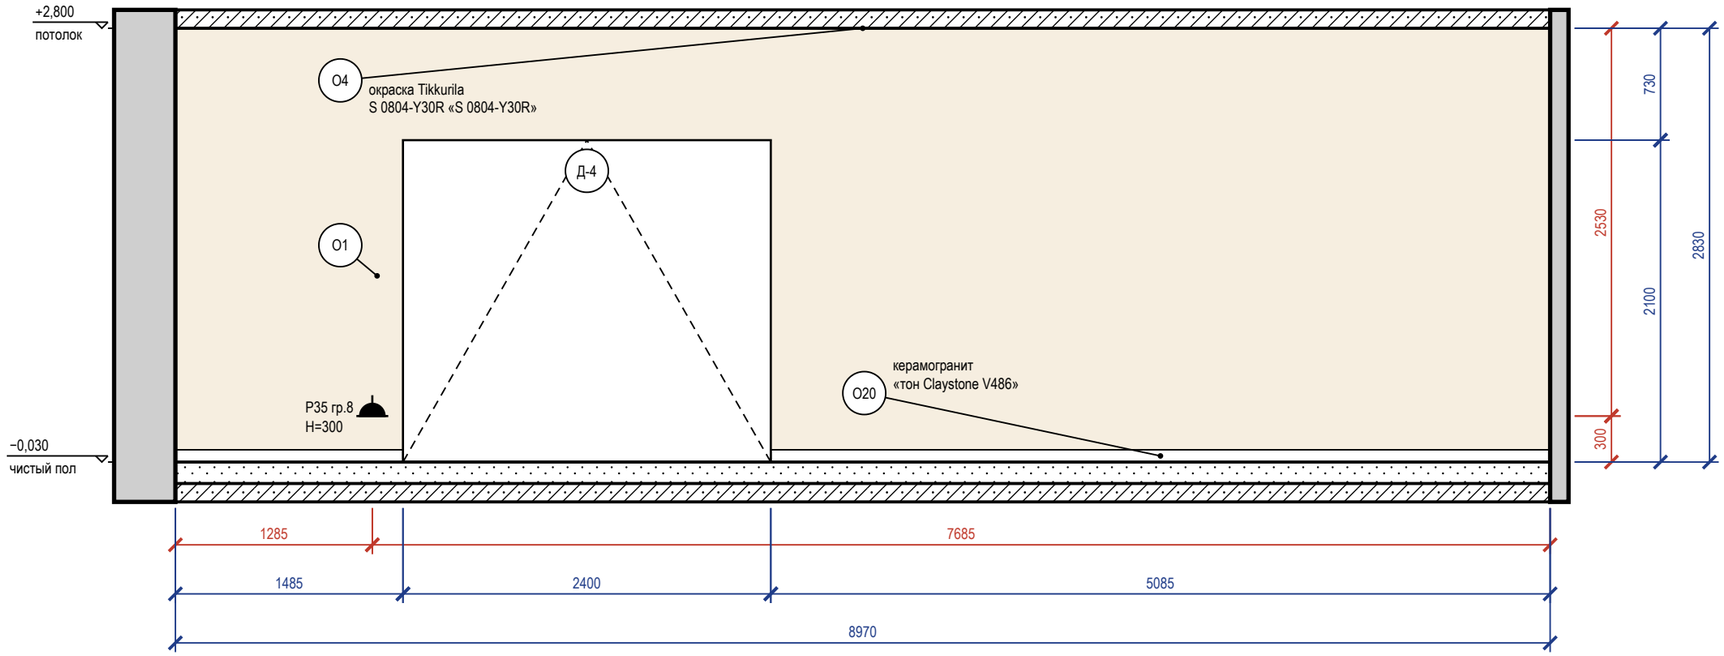


Схема развёрток (М 1:100)

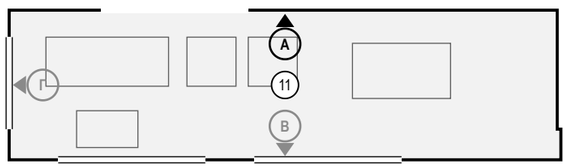

Ведомость отделки (на листе)

Марка	Поверхность	Материал, изделие	Цвет, код	Кол.
О1	стены	окраска, Tikkurila Luja 7, шелковисто-матовая, подготовка К3	NCS S 0804-Y30R «S 0804-Y30R»	20,3 м²
О4	потолок	окраска, Tikkurila Luja 7, матовая, подготовка Q3	NCS S 0804-Y30R «S 0804-Y30R»	21,8 м²
О20	плинтус	керамогранит, аналог: плинтус из керамогранита пола, подрезка 80 мм, верхняя кромка с запилом 45°	#B8AFA5 «тон Claystone V486»	6,6 м

Примечания

1. Размеры — в мм от чистовых поверхностей стен; условные обозначения и общие указания — лист 2.

					Проект: Дом 331 м²
	Лист	№ док.	Подпись	Дата	Развёртка стены А. Веранда (пом. 11)
Дизайнер	Кырлан А.С.			19.10.26	

Стадия	Лист	Листов
П	96	155

выпуск 18.10.2026 № ffc1f29499 · стр. 96 из 155

Развёртка стены В


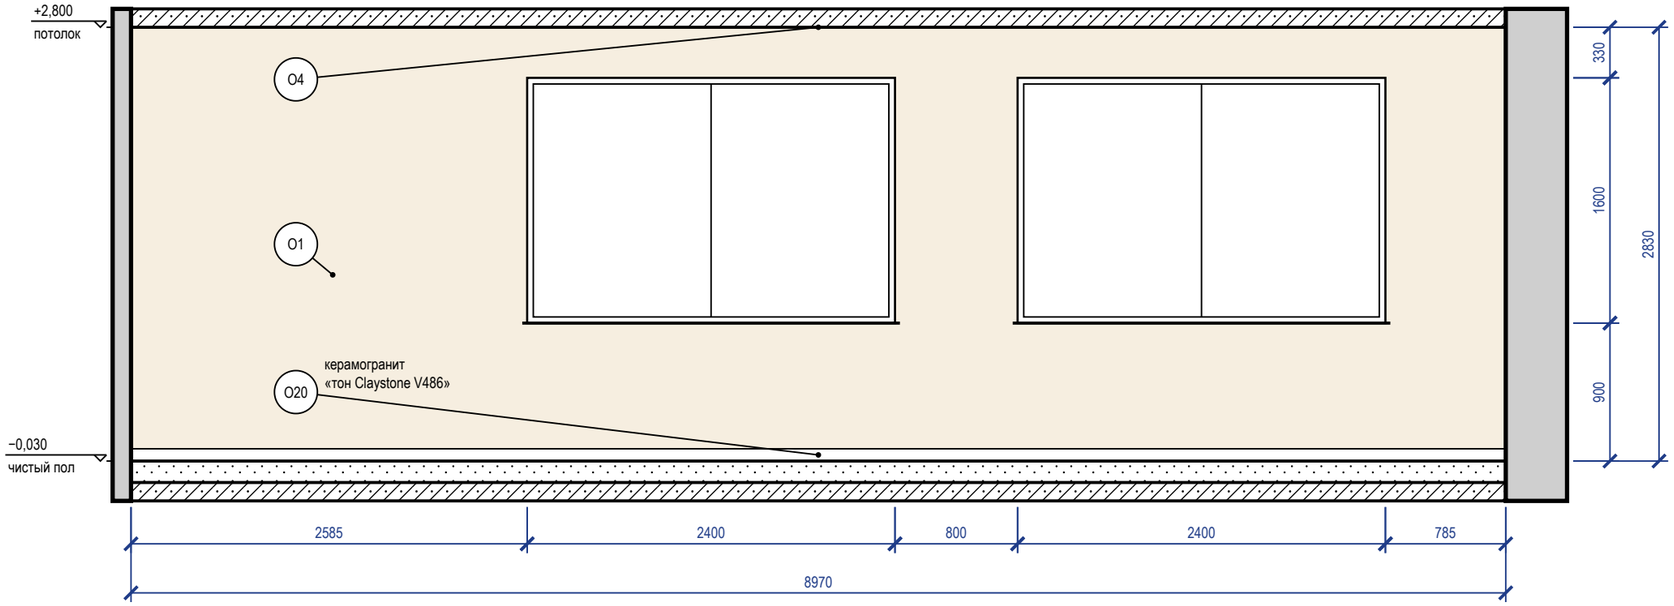


Схема развёрток (М 1:100)

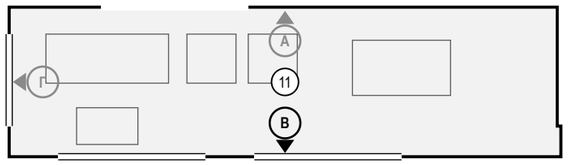

Ведомость отделки (на листе)

Марка	Поверхность	Материал, изделие	Цвет, код	Кол.
О1	стены	окраска, Tikkurila Luja 7, шелковисто-матовая, подготовка К3	NCS S 0804-Y30R «S 0804-Y30R»	17,7 м²
О4	потолок	окраска, Tikkurila Luja 7, матовая, подготовка Q3	NCS S 0804-Y30R «S 0804-Y30R»	21,8 м²
О20	плинтус	керамогранит, аналог: плинтус из керамогранита пола, подрезка 80 мм, верхняя кромка с запилом 45°	#B8AFA5 «тон Claystone V486»	9 м

Визуализация этой стены — лист 95



Примечания

1. Размеры — в мм от чистовых поверхностей стен; условные обозначения и общие указания — лист 2.

					Проект: Дом 331 м²
	Лист	№ док.	Подпись	Дата	
Дизайнер	Кырлан А.С.			19.10.26	Развёртка стены В. Веранда (пом. 11)

Стадия	Лист	Листов
П	97	155

выпуск 18.10.2026 · ffc1f29499 · стр. 97 из 155

Развёртка стены Г


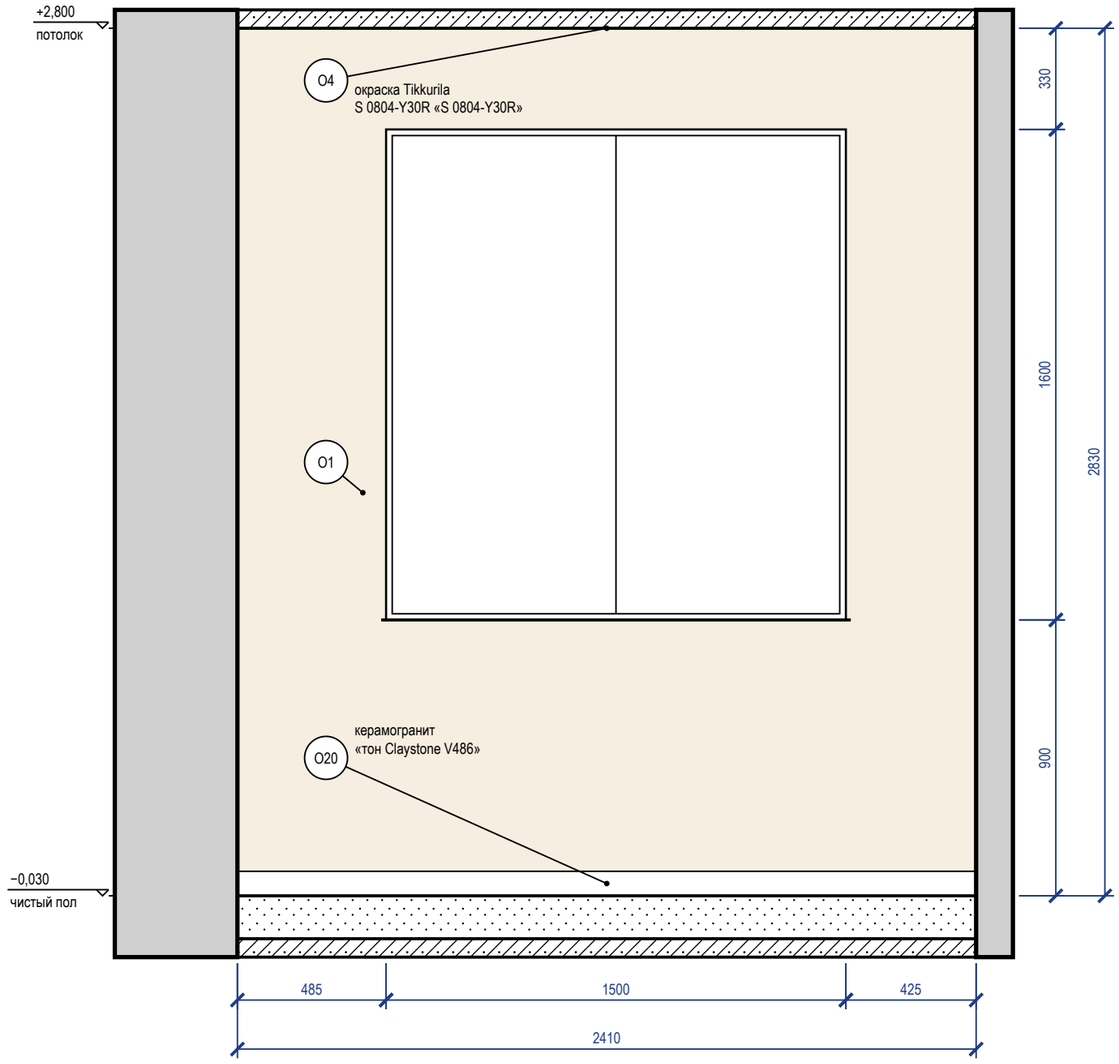


Схема развёрток (М 1:100)

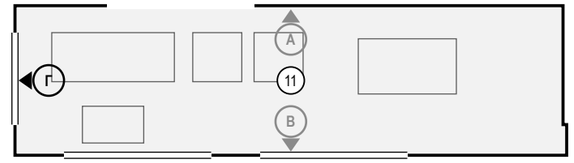

Ведомость отделки (на листе)

Марка	Поверхность	Материал, изделие	Цвет, код	Кол.
О1	стены	окраска, Tikkurila Luja 7, шелковисто-матовая, подготовка К3	NCS S 0804-Y30R «S 0804-Y30R»	4,4 м²
О4	потолок	окраска, Tikkurila Luja 7, матовая, подготовка Q3	NCS S 0804-Y30R «S 0804-Y30R»	21,8 м²
О20	плинтус	керамогранит, аналог: плинтус из керамогранита пола, подрезка 80 мм, верхняя кромка с запилом 45°	#B8AFA5 «тон Claystone V486»	2,4 м

Примечания

1. Размеры — в мм от чистовых поверхностей стен; условные обозначения и общие указания — лист 2.

					Проект: Дом 331 м²
	Лист	№ док.	Подпись	Дата	Развёртка стены Г. Веранда (пом. 11)
Дизайнер	Кырлан А.С.			19.10.26	

Стадия	Лист	Листов
П	98	155

выпуск 18.10.2026 № ffc1f29499 · стр. 98 из 155



					Проект: Дом 331 м²
	Лист	№ док.	Подпись	Дата	Визуализация: Крыльцо
Дизайнер	Кырлан А.С.			19.10.26	

Стадия	Лист	Листов
П	99	155

выпуск 18.10.2026 ffc1f29499 · стр. 99 из 155

Развёртка стены А


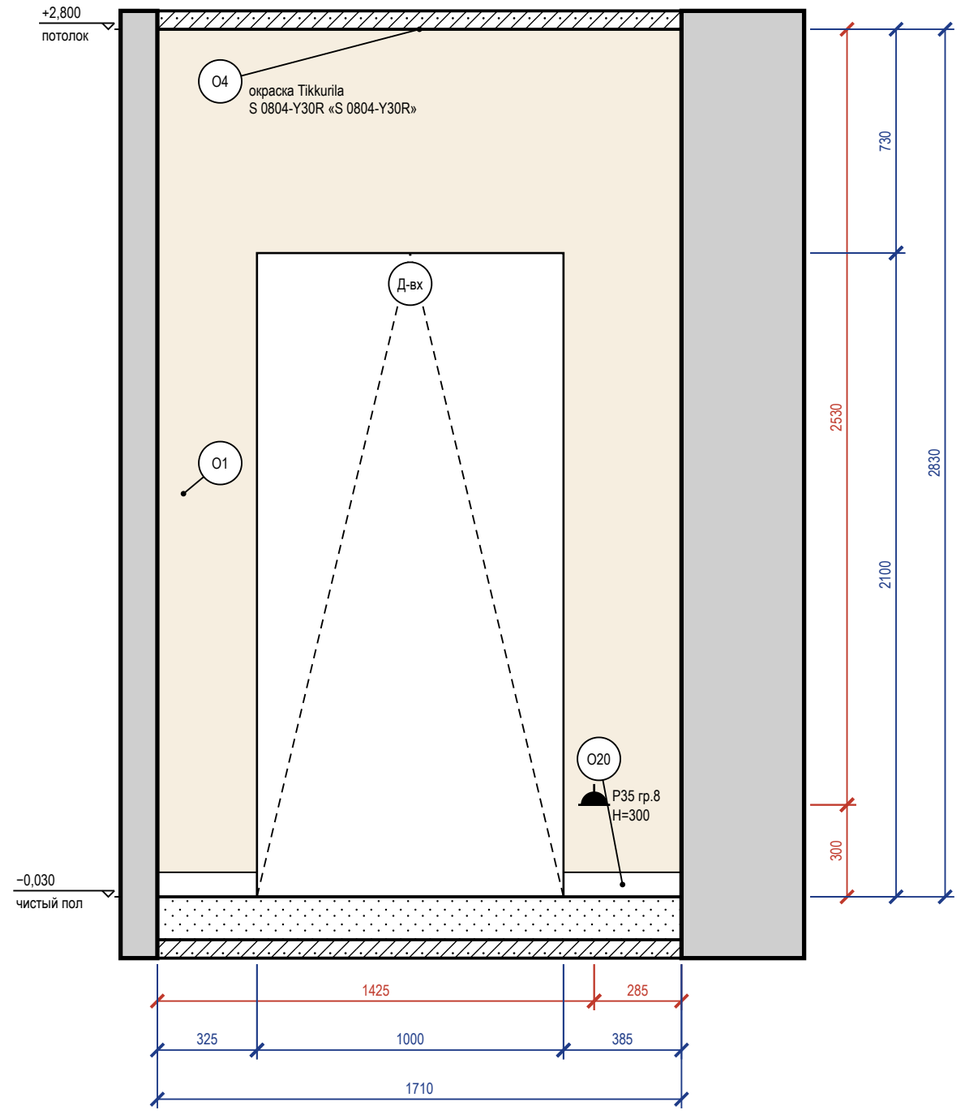


Схема развёрток (М 1:100)

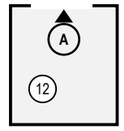

Ведомость отделки (на листе)

Марка	Поверхность	Материал, изделие	Цвет, код	Кол.
О1	стены	окраска, Tikkurila Luja 7, шелковисто-матовая, подготовка К3	NCS S 0804-Y30R «S 0804-Y30R»	2,7 м²
О4	потолок	окраска, Tikkurila Luja 7, матовая, подготовка Q3	NCS S 0804-Y30R «S 0804-Y30R»	3,4 м²
О20	плинтус	керамогранит, аналог: плинтус из керамогранита пола, подрезка 80 мм, верхняя кромка с запилом 45°	#B8AFA5 «тон Claystone V486»	0,7 м

Примечания

1. Размеры — в мм от чистовых поверхностей стен; условные обозначения и общие указания — лист 2.

					Проект: Дом 331 м²
	Лист	№ док.	Подпись	Дата	Развёртки стен. Крыльцо (пом. 12)
Дизайнер	Кырлан А.С.			19.10.26	

Стадия	Лист	Листов
П	100	155

выпуск 18.10.2026 № ffc1f29499 · стр. 100 из 155



					Проект: Дом 331 м²	
	Лист	№ док.	Подпись	Дата		
Дизайнер	Кырлан А.С.			19.10.26	Визуализация: Спальня мастер	Стадия / Лист / Листов
						П / 101 / 155

выпуск 18.10.2026 № ffc1f29499 · стр. 101 из 155



					Проект: Дом 331 м²
	Лист	№ док.	Подпись	Дата	
Дизайнер	Кырлан А.С.			19.10.26	Визуализация: Спальня мастер

Стадия	Лист	Листов
П	102	155

выпуск 18.10.2026 № ffc1f29499 · стр. 102 из 155

Развёртка стены А


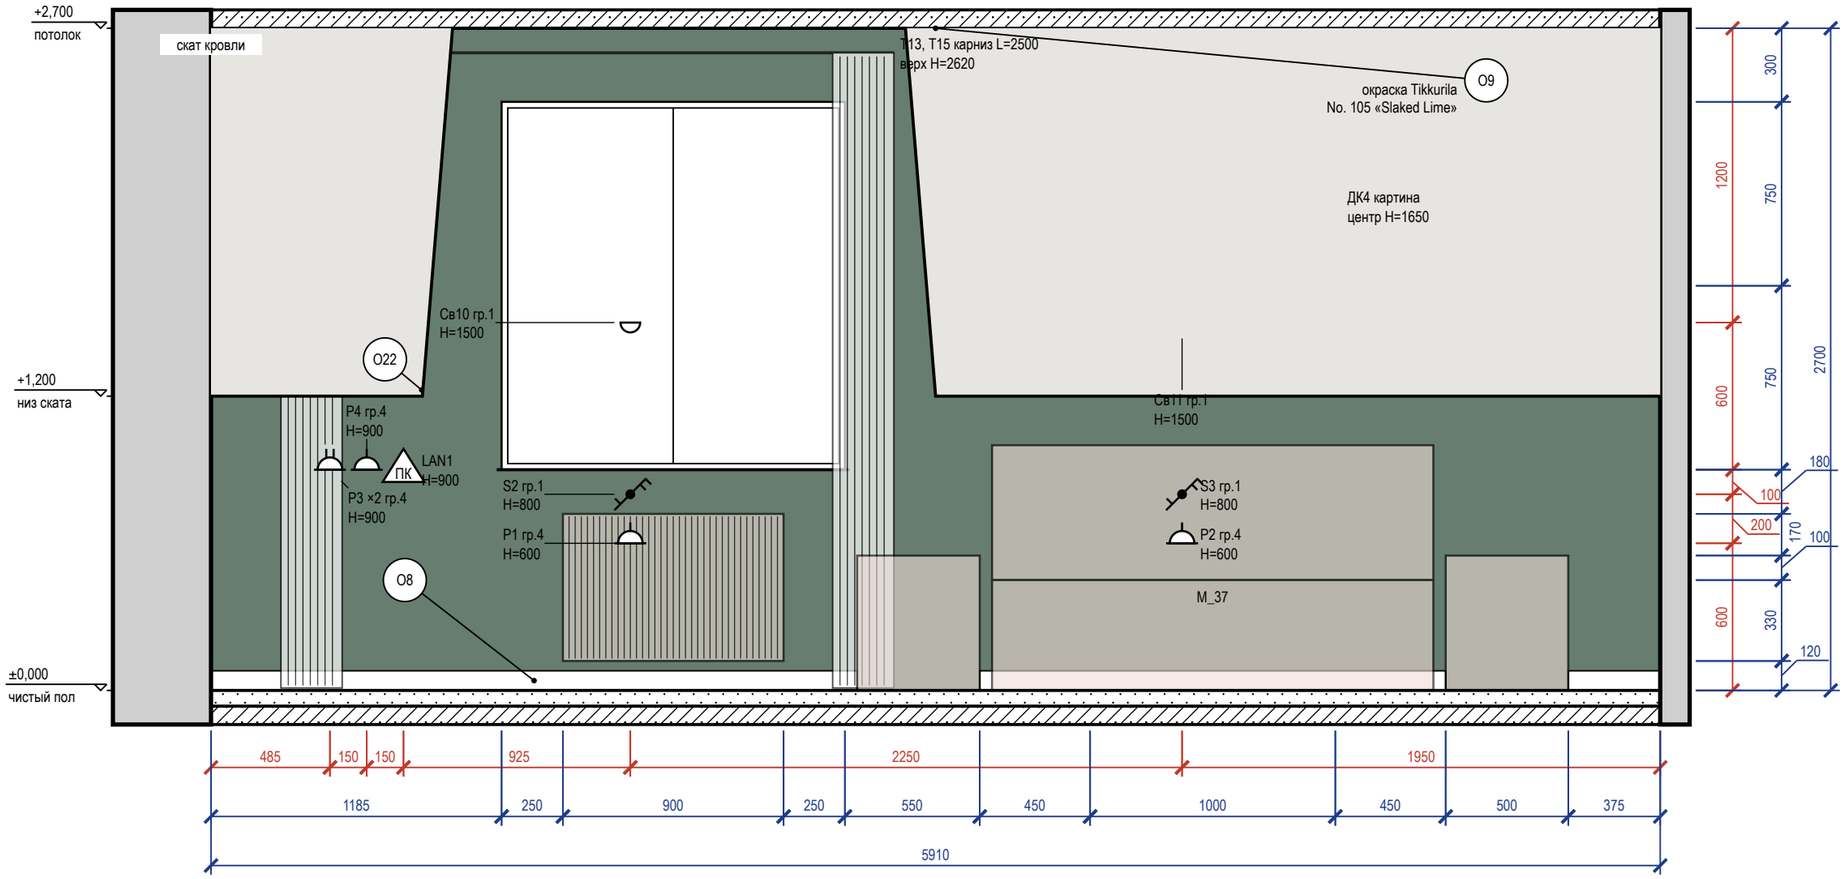


Схема развёрток (М 1:100)

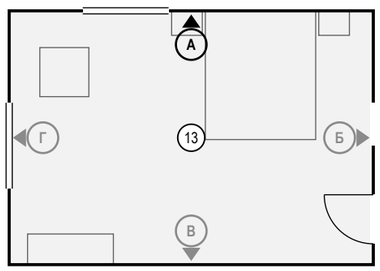

Ведомость отделки (на листе)

Марка	Поверхность	Материал, изделие	Цвет, код	Кол.
О8	плинтус	плинтус МДФ, h 80 мм, аналог: плинтус МДФ под покраску 80×16	Farrow & Ball No. 226 «Joa's White»	4,9 м
О9	потолок	окраска, Tikkurila Anti-Reflex 2, глубокоматовая, подготовка Q3	Little Greene No. 105 «Slaked Lime»	24,6 м²
О22	акцентная стена	окраска, Farrow & Ball Modern Emulsion, матовая, подготовка Q3	NCS S 7020-G10Y «Хвойный тёмно-зелёный»	13,9 м²

Визуализация этой стены



Примечания

1. Размеры — в мм от чистовых поверхностей стен; условные обозначения и общие указания — лист 2.
2. Картины и зеркала крепить к основанию по паспорту изделия (закладные и анкеры — в перечне скрытых работ); крест — ось центра предмета.
3. Карнизы (шины) — по ведомости текстиля декоратора; длина L и верх H — по развёртке, крепление — до окраски потолка.
4. Линии узора (швы плитки, складки штор, рёбра радиаторов) прерываются у знаков и выносок — просвет между линиями не менее 0,7 мм.

					Проект: Дом 331 м²
	Лист	№ док.	Подпись	Дата	
Дизайнер	Кырлан А.С.			19.10.26	Развёртка стены А. Спальня мастер (пом. 13)

Стадия	Лист	Листов
П	103	155

выпуск 18.10.2026 № ffc1f29499 · стр. 103 из 155

Развёртка стены Б


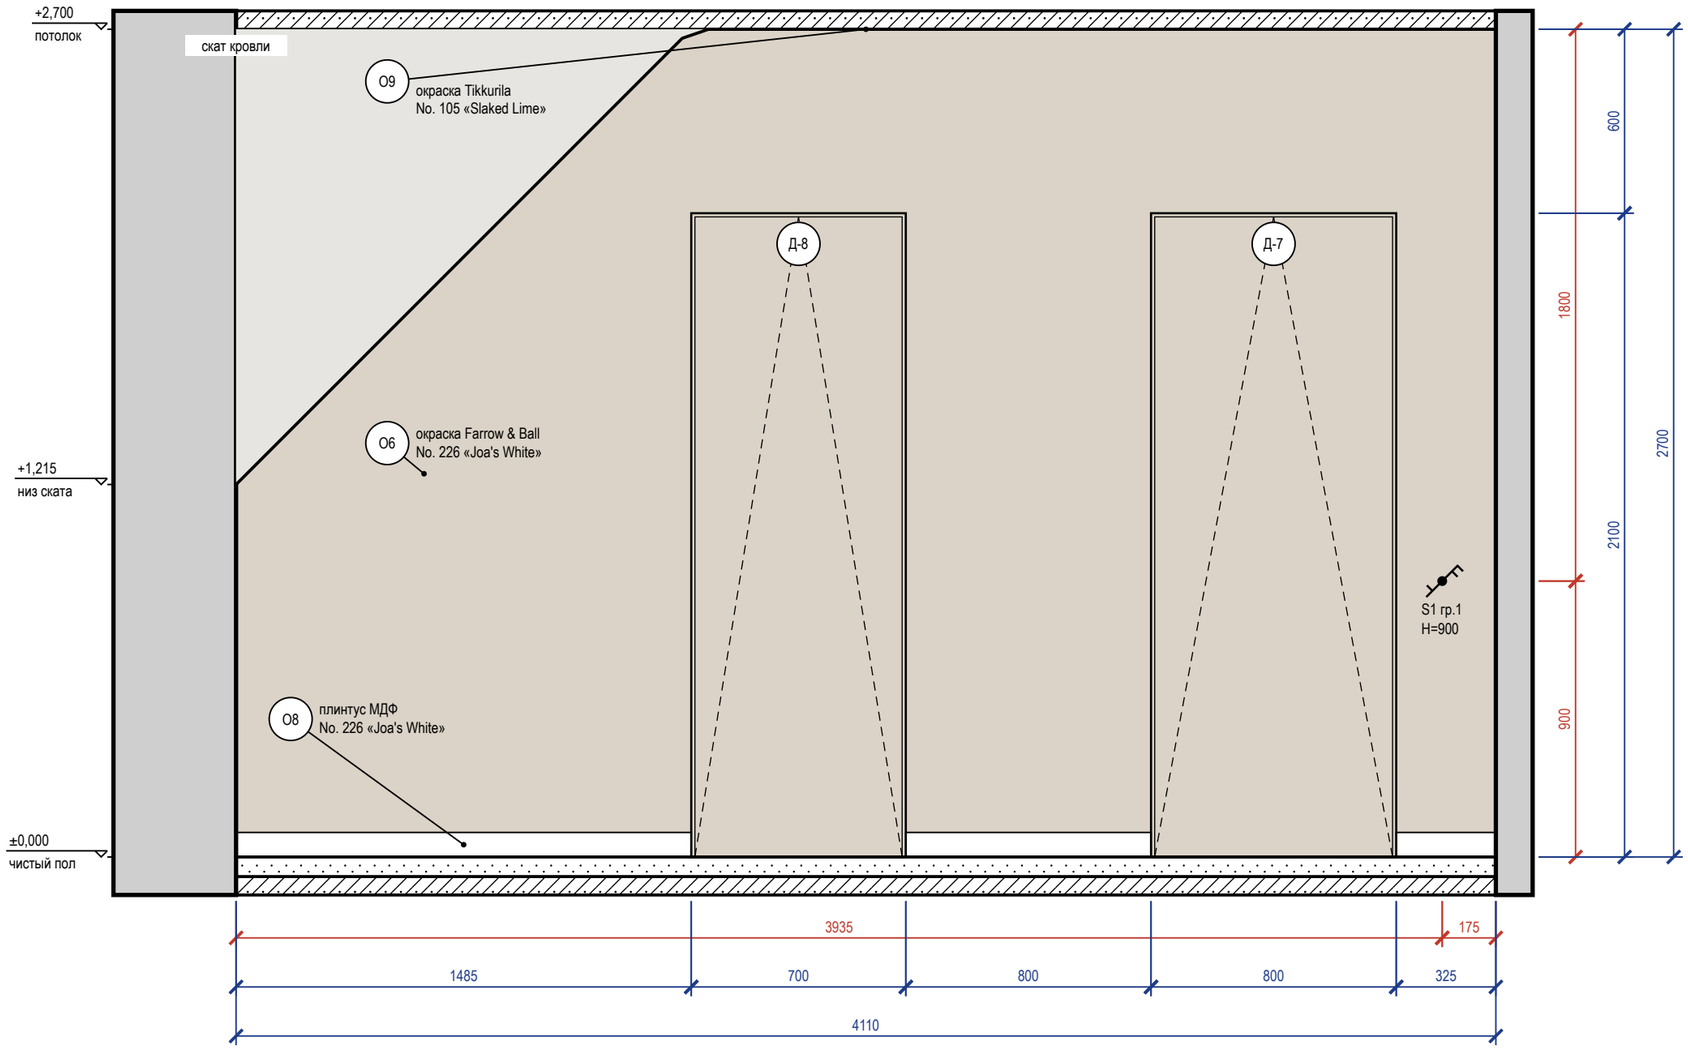


Схема развёрток (М 1:100)

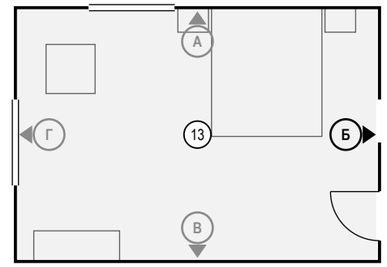

Ведомость отделки (на листе)

Марка	Поверхность	Материал, изделие	Цвет, код	Кол.
О6	стены	окраска, Farrow & Ball Modern Emulsion, матовая, подготовка Q3	Farrow & Ball No. 226 «Joa's White»	7,9 м²
О8	плинтус	плинтус МДФ, h 80 мм, аналог: плинтус МДФ под покраску 80×16	Farrow & Ball No. 226 «Joa's White»	2,6 м
О9	потолок	окраска, Tikkurila Anti-Reflex 2, глубокоматовая, подготовка Q3	Little Greene No. 105 «Slaked Lime»	24,6 м²

Примечания

1. Размеры — в мм от чистовых поверхностей стен; условные обозначения и общие указания — лист 2.
2. Двери скрытого монтажа — полотно в плоскости стены, отделка стены по полотну, плинтус прерывается у короба (узел — на листе узлов).

	Лист	№ док.	Подпись	Дата
Дизайнер	Кырлан А.С.			19.10.26

Проект: Дом 331 м²

Развёртка стены Б. Спальня мастер (пом. 13)

Стадия	Лист	Листов
П	104	155

выпуск 18.10.2026 № ffc1f29499 · стр. 104 из 155

Развёртка стены В


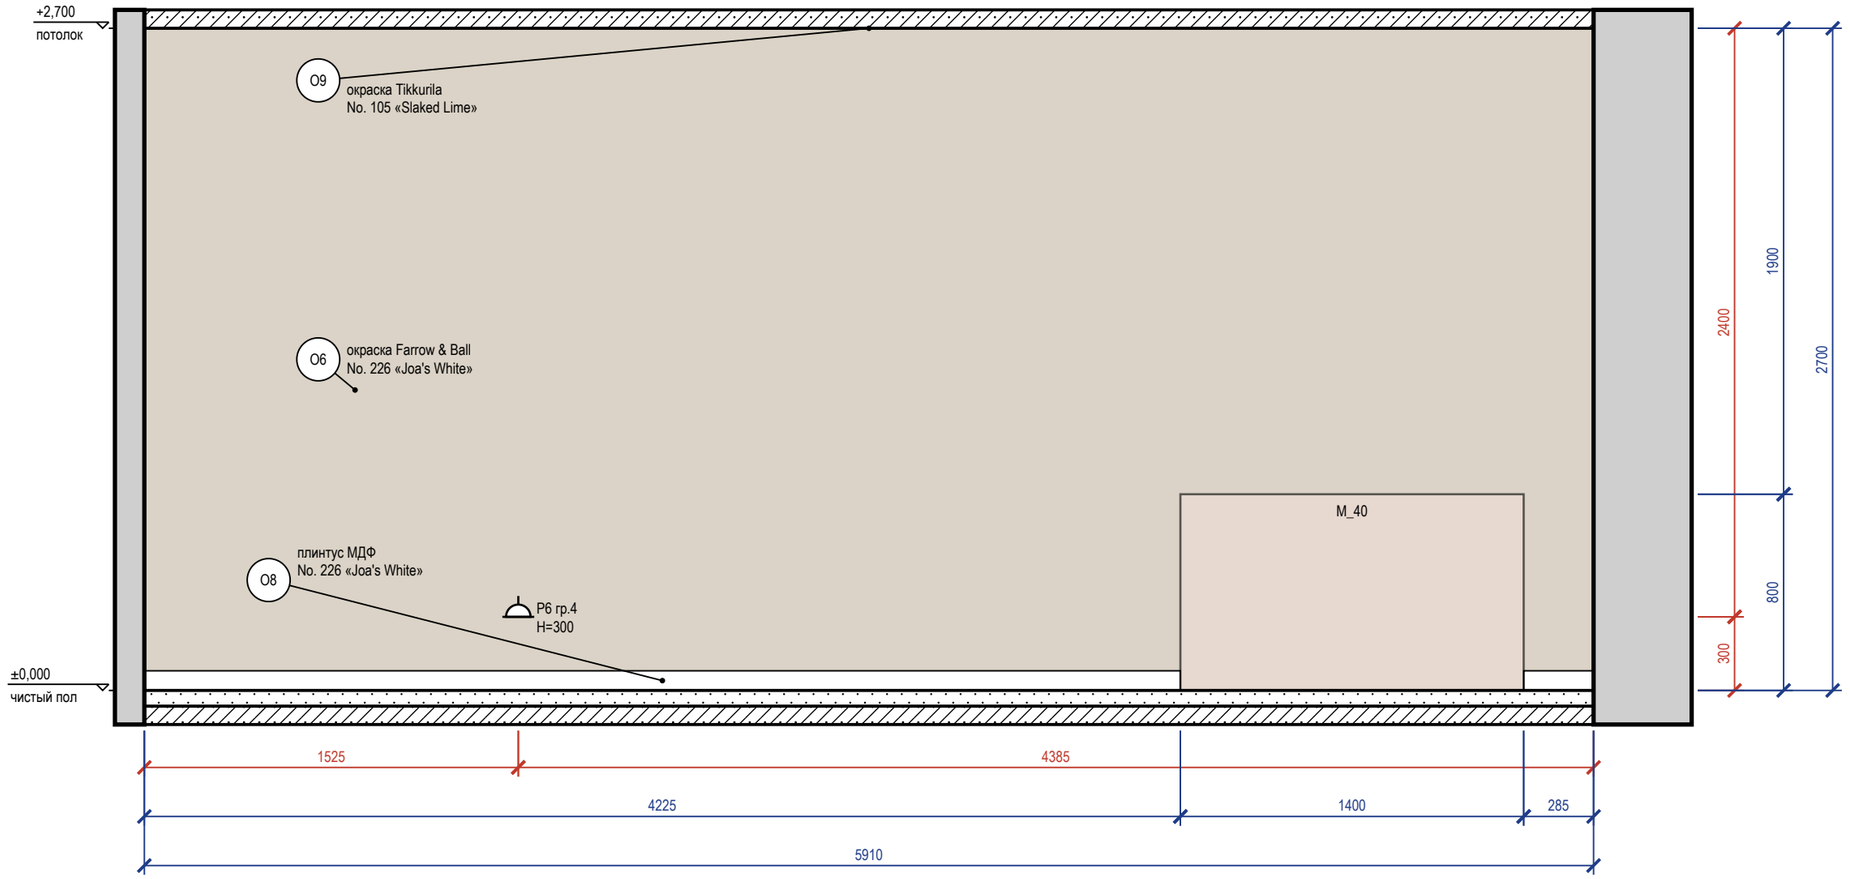



Схема развёрток (М 1:100)

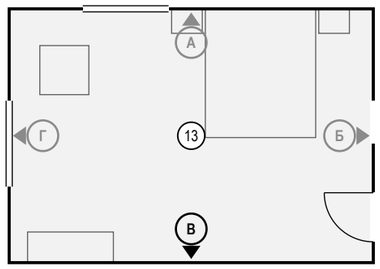

Ведомость отделки (на листе)

Марка	Поверхность	Материал, изделие	Цвет, код	Кол.
О6	стены	окраска, Farrow & Ball Modern Emulsion, матовая, подготовка Q3	Farrow & Ball No. 226 «Joa's White»	16 м²
О8	плинтус	плинтус МДФ, h 80 мм, аналог: плинтус МДФ под покраску 80×16	Farrow & Ball No. 226 «Joa's White»	4,5 м
О9	потолок	окраска, Tikkurila Anti-Reflex 2, глубокоматовая, подготовка Q3	Little Greene No. 105 «Slaked Lime»	24,6 м²

Визуализация этой стены — лист 102

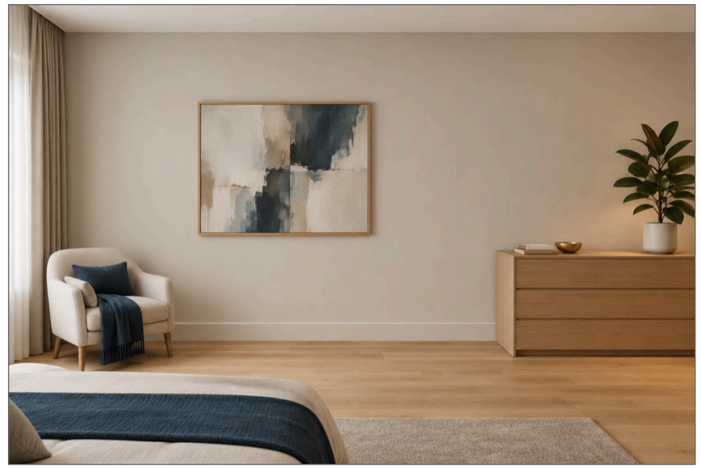

Примечания

1. Размеры — в мм от чистовых поверхностей стен; условные обозначения и общие указания — лист 2.

					Проект: Дом 331 м²
	Лист	№ док.	Подпись	Дата	Развёртка стены В. Спальня мастер (пом. 13)
Дизайнер	Кырлан А.С.			19.10.26	

Стадия	Лист	Листов
П	105	155

выпуск 18.10.2026 № ffc1f29499 · стр. 105 из 155

Развёртка стены Г


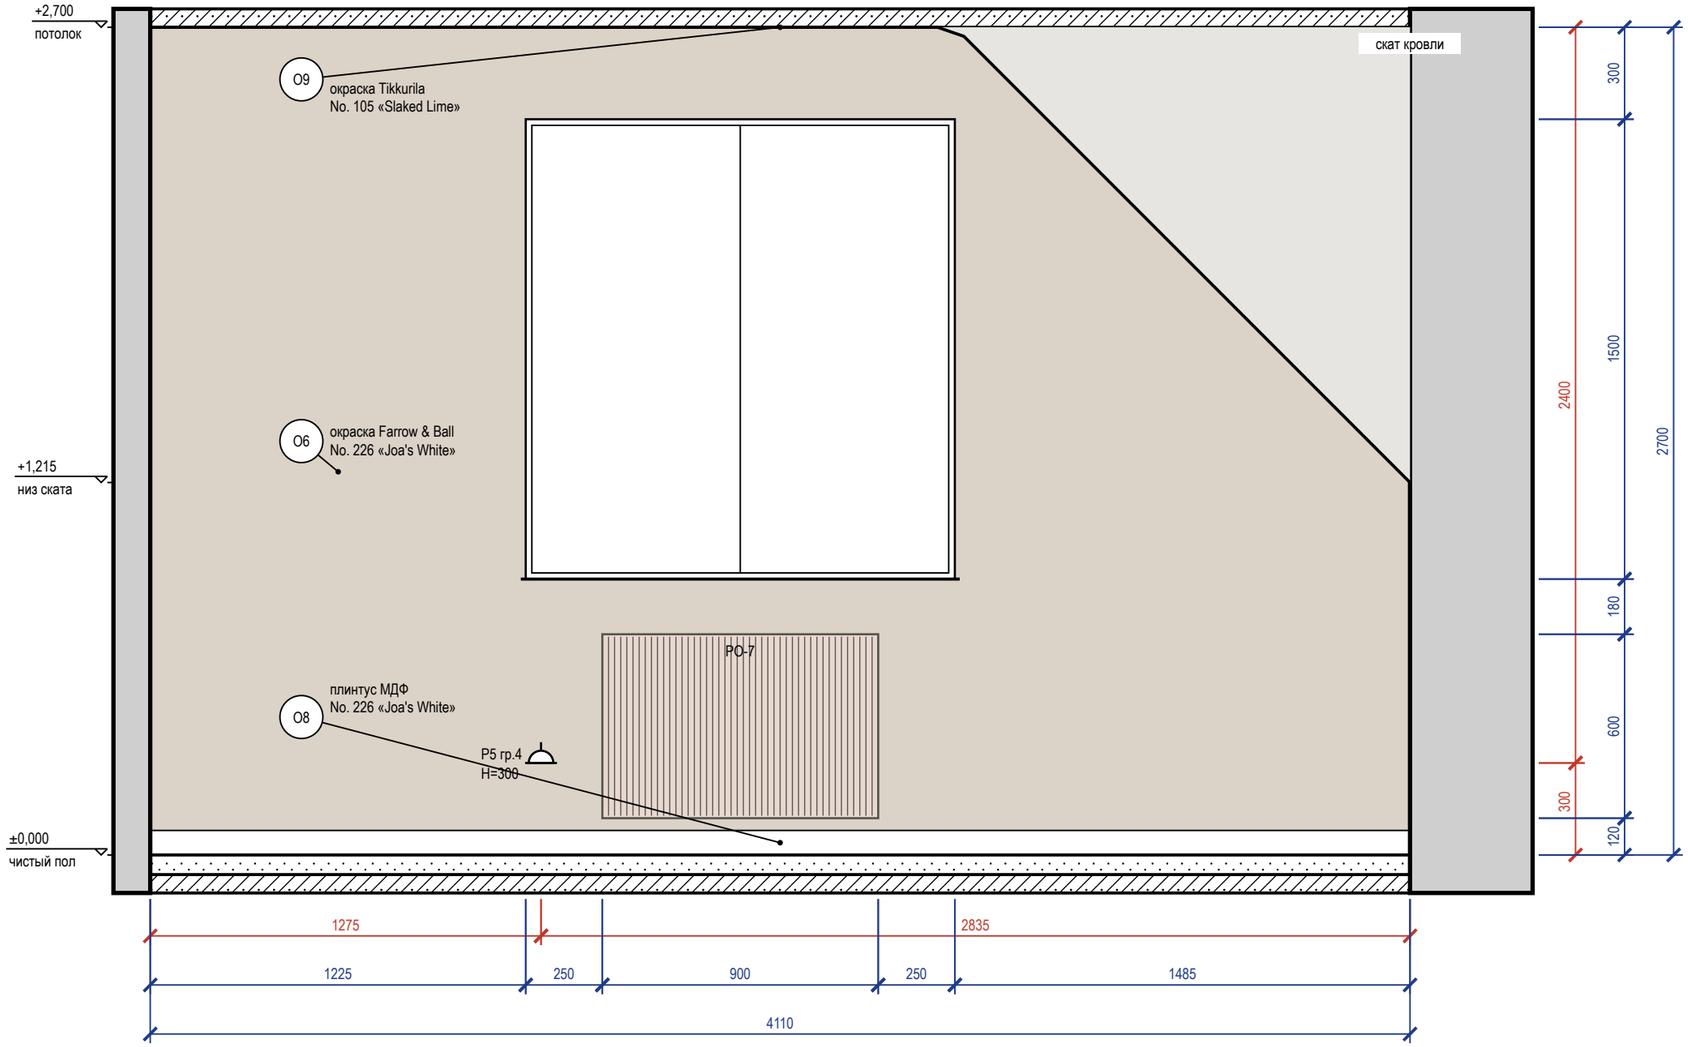


Схема развёрток (М 1:100)



Визуализация этой стены

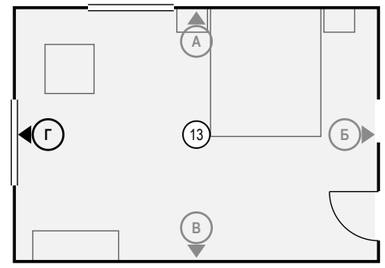

Ведомость отделки (на листе)

Марка	Поверхность	Материал, изделие	Цвет, код	Кол.
О6	стены	окраска, Farrow & Ball Modern Emulsion, матовая, подготовка Q3	Farrow & Ball No. 226 «Joa's White»	9 м²
О8	плинтус	плинтус МДФ, h 80 мм, аналог: плинтус МДФ под покраску 80×16	Farrow & Ball No. 226 «Joa's White»	4,1 м
О9	потолок	окраска, Tikkurila Anti-Reflex 2, глубокоматовая, подготовка Q3	Little Greene No. 105 «Slaked Lime»	24,6 м²

Примечания

1. Размеры — в мм от чистовых поверхностей стен; условные обозначения и общие указания — лист 2.

					Проект: Дом 331 м²
	Лист	№ док.	Подпись	Дата	Развёртка стены Г. Спальня мастер (пом. 13)
Дизайнер	Кырлан А.С.			19.10.26	

Стадия	Лист	Листов
П	106	155

выпуск 18.10.2026 № ffc1f29499 · стр. 106 из 155




					Проект: Дом 331 м²
	Лист	№ док.	Подпись	Дата	
Дизайнер	Кырлан А.С.			19.10.26	Визуализация: Гардеробная мастер

Стадия	Лист	Листов
П	107	155

выпуск 18.10.2026 № ffc1f29499 · стр. 107 из 155

Развёртка стены А

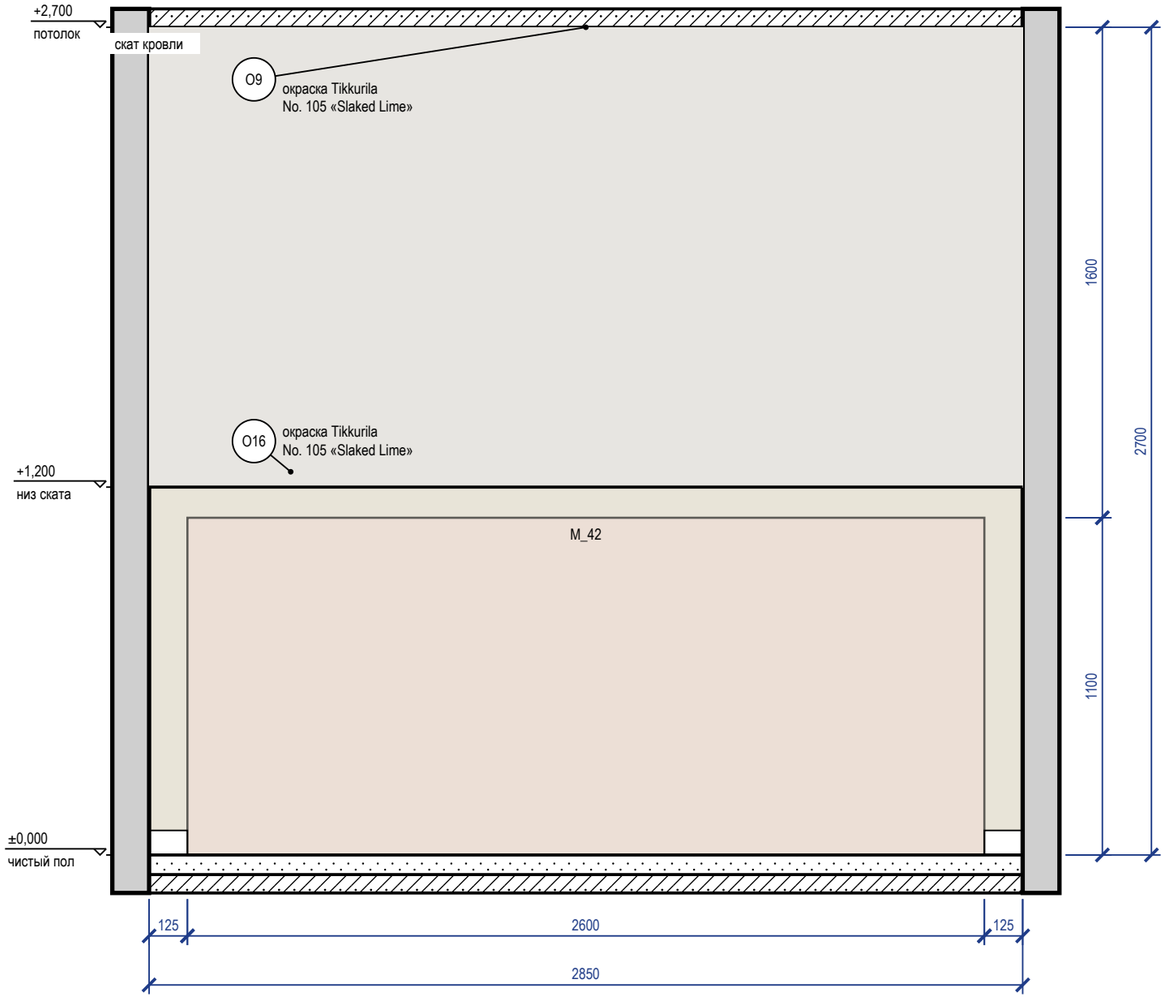

Развёртка стены Б


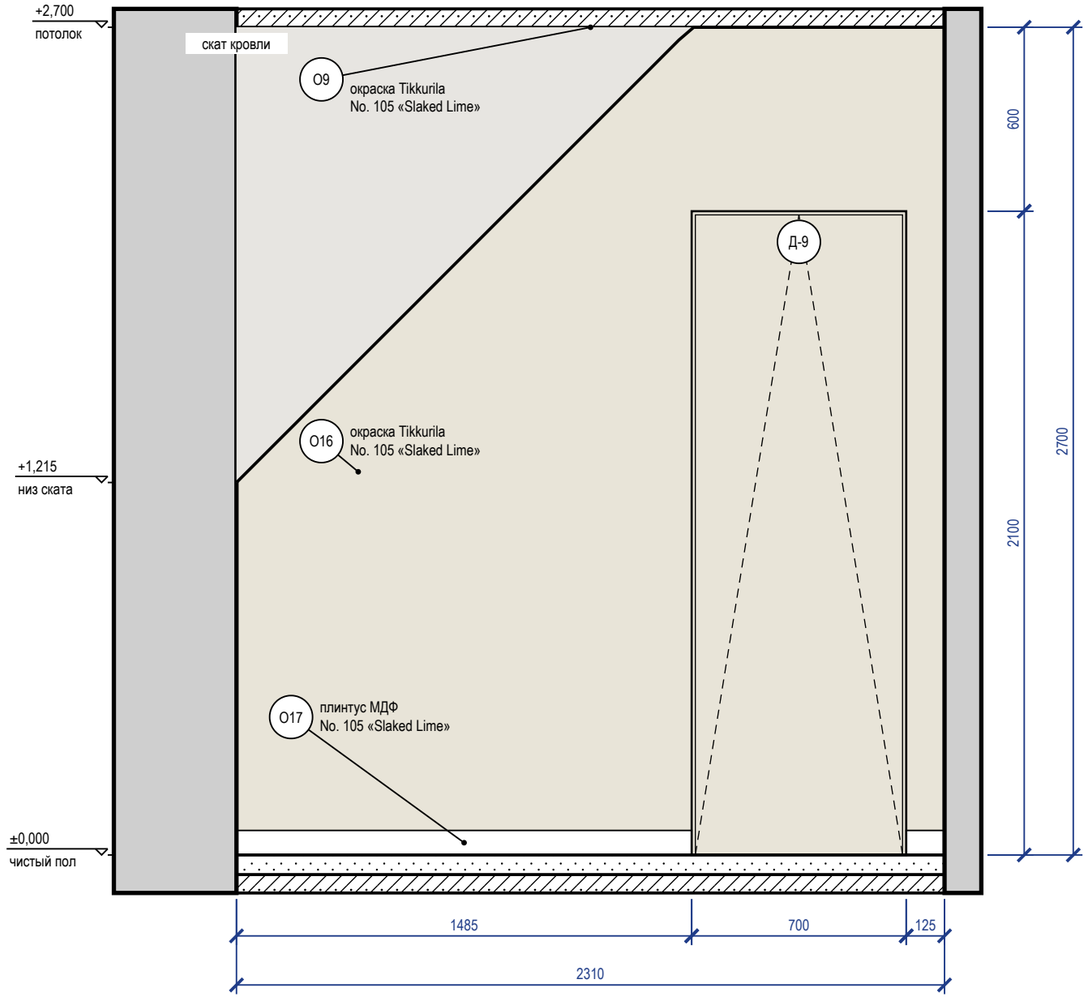



Схема развёрток (М 1:100)

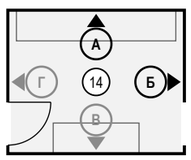

Ведомость отделки (на листе)

Марка	Поверхность	Материал, изделие	Цвет, код	Кол.
О9	потолок	окраска, Tikkurila Anti-Reflex 2, глубокоматовая, подготовка Q3	Little Greene No. 105 «Slaked Lime»	6,7 м²
О16	стены	окраска, Tikkurila Harmony, матовая, подготовка Q3	Little Greene No. 105 «Slaked Lime»	12,5 м²
О17	плинтус	плинтус МДФ, h 80 мм, аналог: плинтус МДФ под покраску 80×16	Little Greene No. 105 «Slaked Lime»	1,9 м

Визуализация этой стены

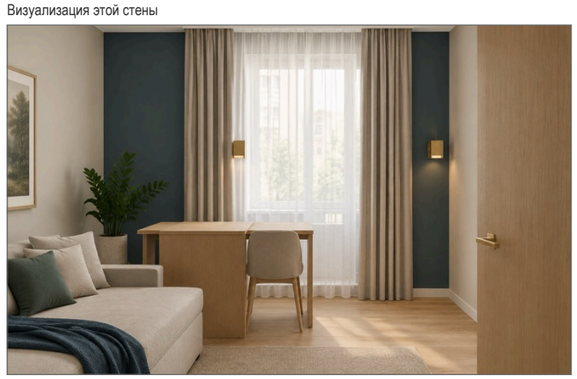

Примечания


1. Размеры — в мм от чистовых поверхностей стен; условные обозначения и общие указания — лист 2.
2. Двери скрытого монтажа — полотно в плоскости стены, отделка стены по полотну, плинтус прерывается у короба (узел — на листе узлов).

					Проект: Дом 331 м²
	Лист	№ док.	Подпись	Дата	Развёртки стен А, Б. Гардеробная мастер (пом. 14)
Дизайнер	Кырлан А.С.			19.10.26	

Стадия	Лист	Листов
П	108	155

выпуск 18.10.2026 № ffc1f29499 · стр. 108 из 155

Развёртка стены В

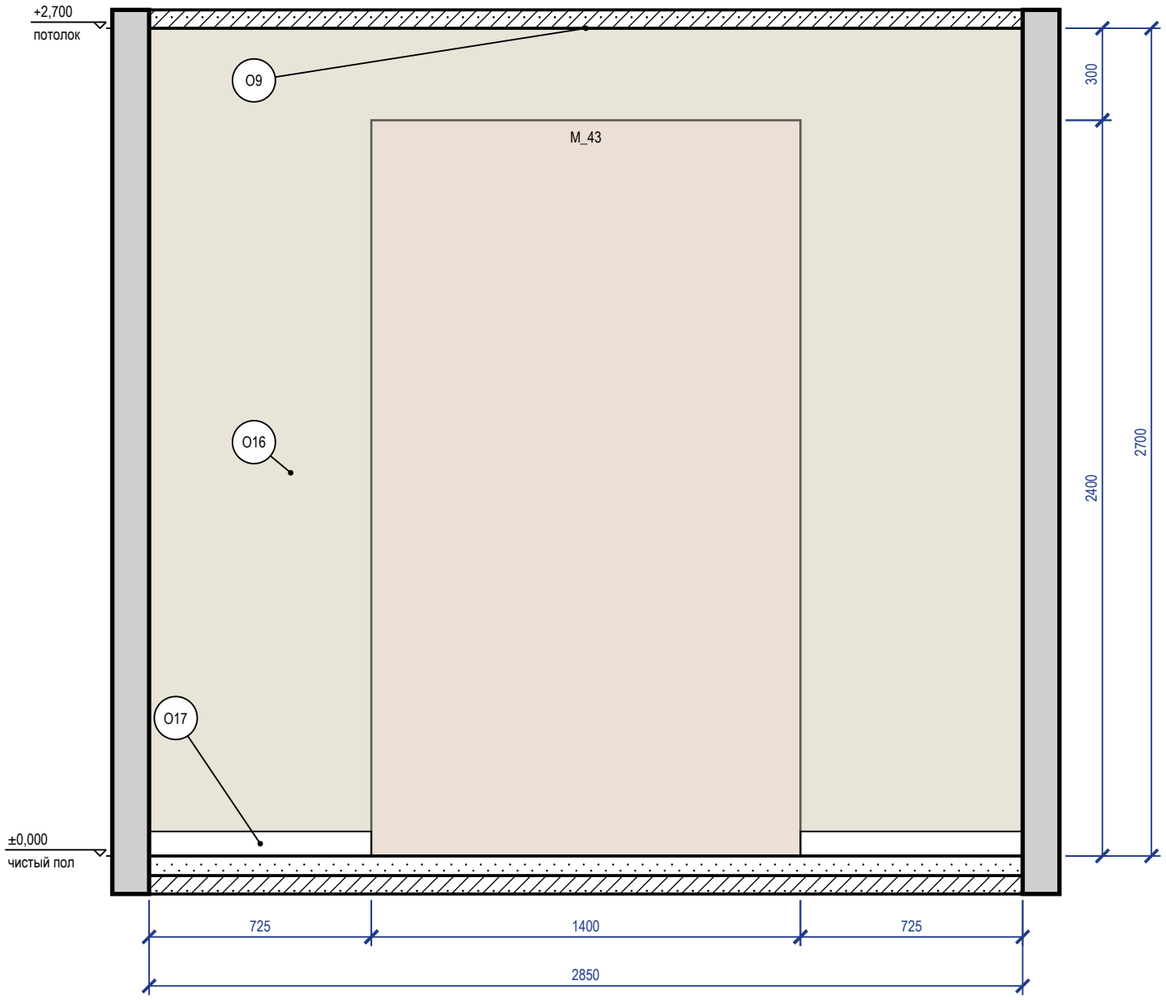

Развёртка стены Г


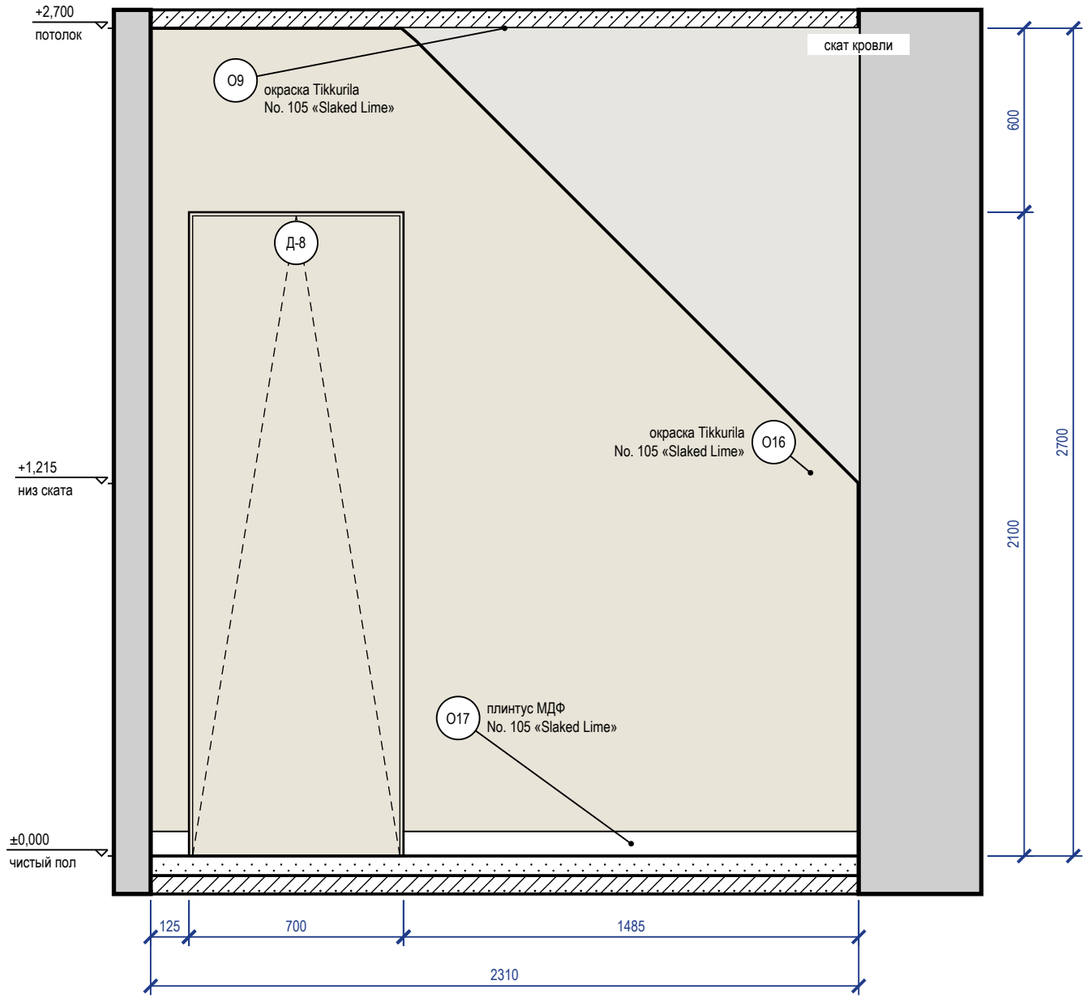


Схема развёрток (М 1:100)

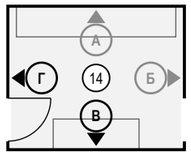

Ведомость отделки (на листе)

Марка	Поверхность	Материал, изделие	Цвет, код	Кол.
О9	потолок	окраска, Tikkurila Anti-Reflex 2, глубокоматовая, подготовка Q3	Little Greene No. 105 «Slaked Lime»	6,7 м²
О16	стены	окраска, Tikkurila Harmony, матовая, подготовка Q3	Little Greene No. 105 «Slaked Lime»	12,5 м²
О17	плинтус	плинтус МДФ, h 80 мм, аналог: плинтус МДФ под покраску 80×16	Little Greene No. 105 «Slaked Lime»	3,1 м

Визуализация этой стены



Примечания

1. Размеры — в мм от чистовых поверхностей стен; условные обозначения и общие указания — лист 2.
2. Двери скрытого монтажа — полотно в плоскости стены, отделка стены по полотну, плинтус прерывается у короба (узел — на листе узлов).

					Проект: Дом 331 м²
	Лист	№ док.	Подпись	Дата	Развёртки стен В, Г. Гардеробная мастер (пом. 14)
Дизайнер	Кырлан А.С.			19.10.26	

Стадия	Лист	Листов
П	109	155

выпуск 18.10.2026 № ffc1f29499 · стр. 109 из 155



					Проект: Дом 331 м²
	Лист	№ док.	Подпись	Дата	
Дизайнер	Кырлан А.С.			19.10.26	Визуализация: Санузел мастер

Стадия	Лист	Листов
П	110	155

выпуск 18.10.2026 № ffc1f29499 · стр. 110 из 155

Развёртка стены А


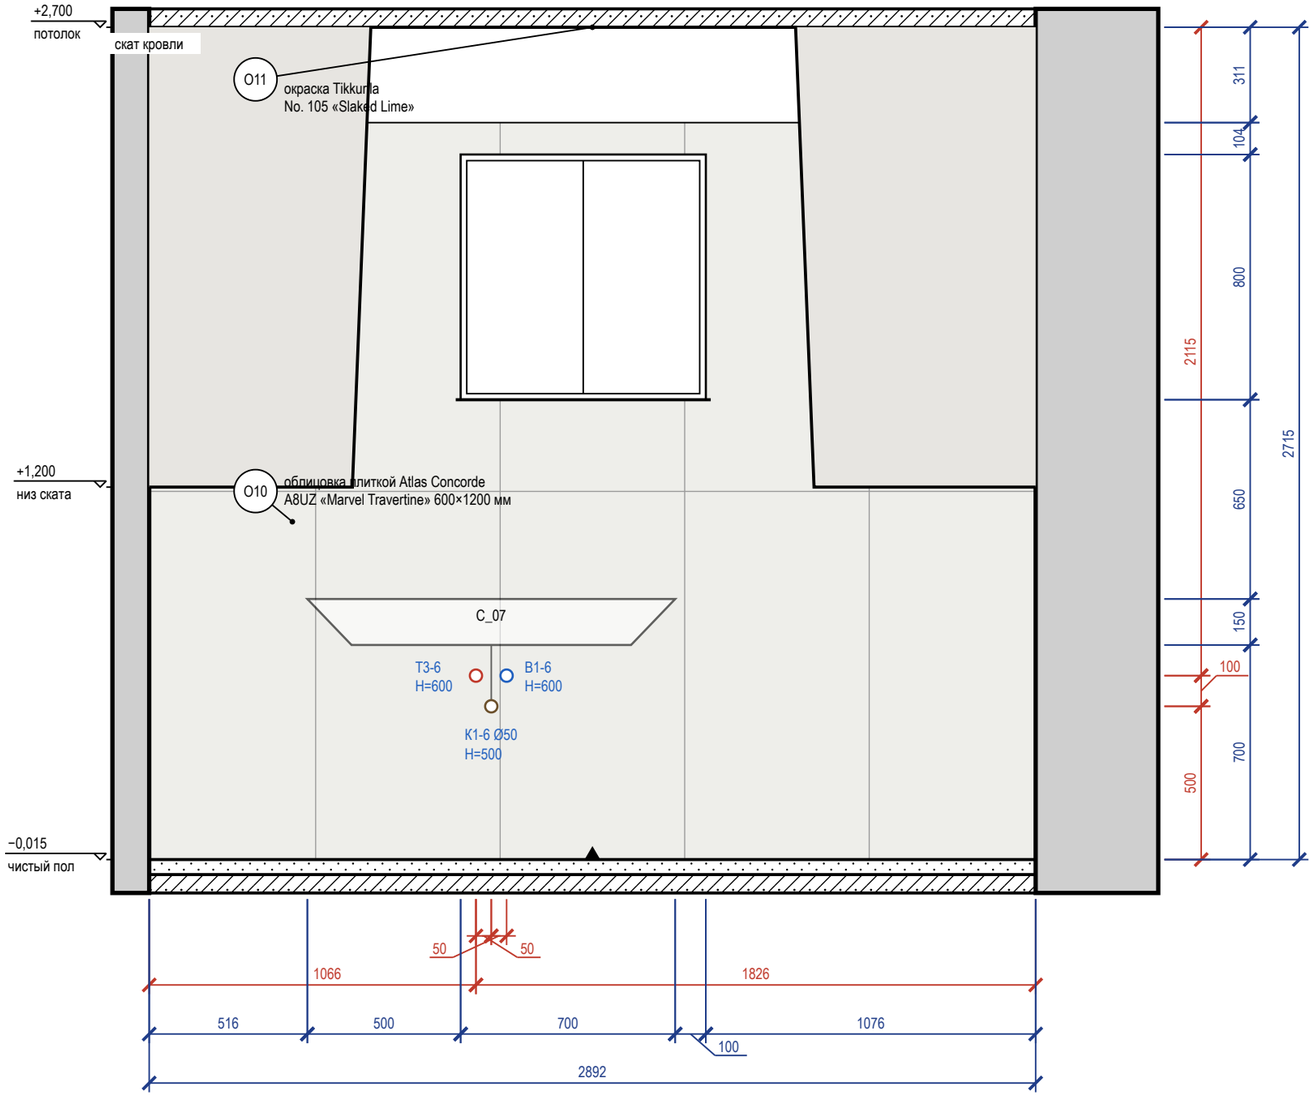


Схема развёрток (М 1:100)

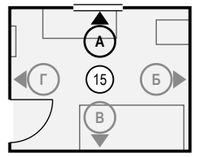

Ведомость отделки (на листе)

Марка	Поверхность	Материал, изделие	Цвет, код	Кол.
О10	стены	облицовка плиткой, Atlas Concorde Marvel Travertine, 600×1200×9 мм, A8UZ, затирка CG2WA	Atlas Concorde A8UZ «Marvel Travertine»	6,3 м²
О11	потолок	окраска, Tikkurila Luja 7, матовая, подготовка Q3	Little Greene No. 105 «Slaked Lime»	6,9 м²

Примечания

1. Размеры — в мм от чистовых поверхностей стен; условные обозначения и общие указания — лист 2.
2. Схема мебели, приборов и декора не является технической документацией для производства мебели; габариты — по паспортам изделий.
3. Выводы ВК — коды и высоты по листу выводов сантехники.
4. Облицовка — по сетке швов 2 мм, раскладка от оси стены (треугольник у пола), целые ряды от пола; подрезки — по листу раскладки плитки.
5. Гидроизоляция в 2 слоя, заход на стены 200 мм — до облицовки, с актом скрытых работ и тестом проливом (узел — на листе узлов).

					Проект: Дом 331 м²
	Лист	№ док.	Подпись	Дата	Развёртка стены А. Санузел мастер (пом. 15)
Дизайнер	Кырлан А.С.			19.10.26	

Стадия	Лист	Листов
П	111	155

выпуск 18.10.2026 № ffc1f29499 · стр. 111 из 155

Развёртка стены Б


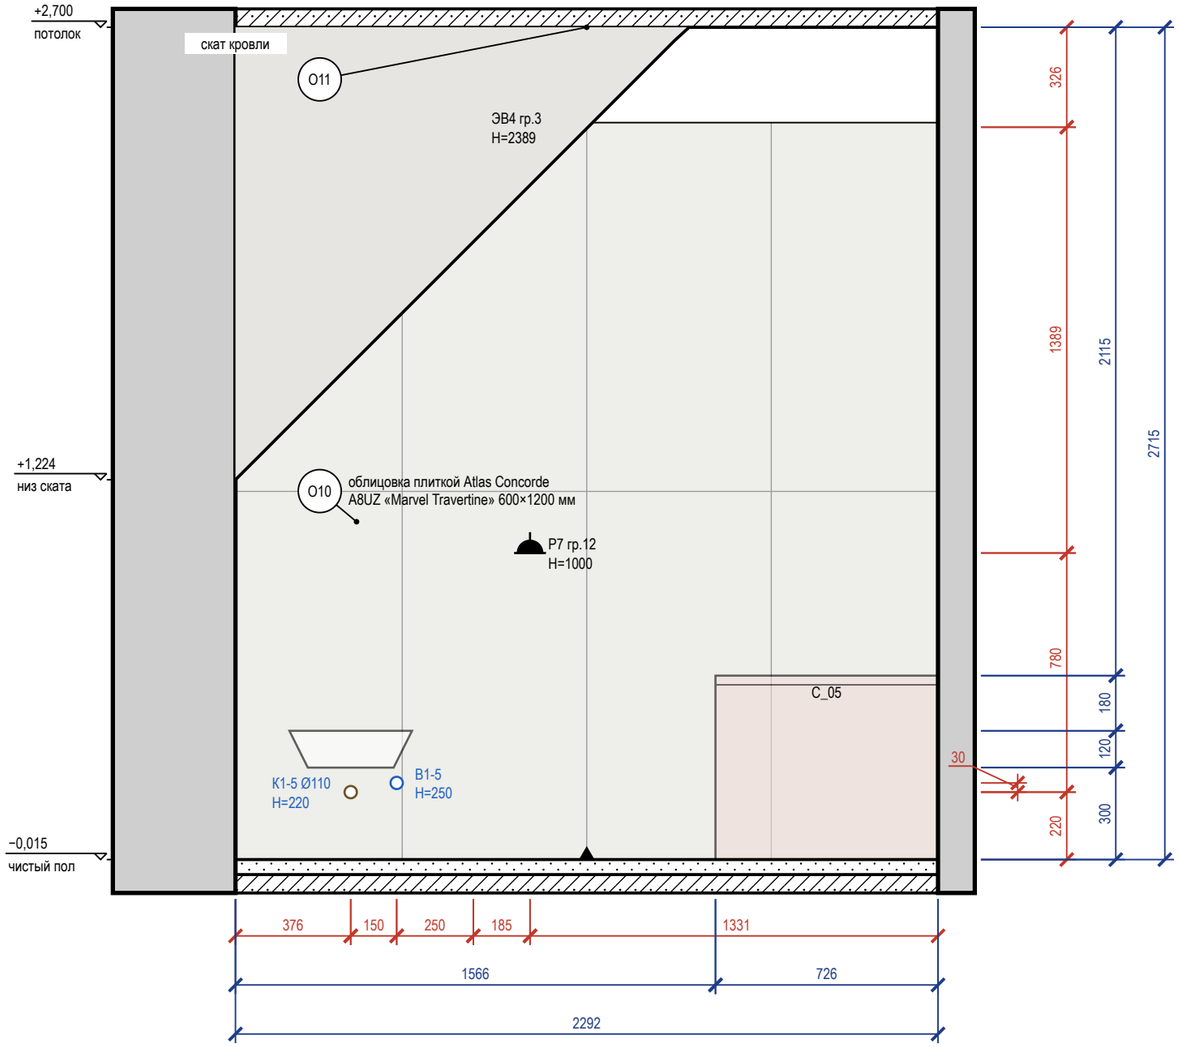


Схема развёрток (М 1:100)

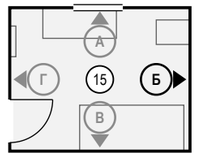

Ведомость отделки (на листе)

Марка	Поверхность	Материал, изделие	Цвет, код	Кол.
О10	стены	облицовка плиткой, Atlas Concorde Marvel Travertine, 600×1200×9 мм, A8UZ, затирка CG2WA	Atlas Concorde A8UZ «Marvel Travertine»	5,5 м²
О11	потолок	окраска, Tikkurila Luja 7, матовая, подготовка Q3	Little Greene No. 105 «Slaked Lime»	6,9 м²

Визуализация этой стены — лист 110



Примечания

1. Размеры — в мм от чистовых поверхностей стен; условные обозначения и общие указания — лист 2.
2. Схема мебели, приборов и декора не является технической документацией для производства мебели; габариты — по паспортам изделий.
3. Выводы ВК — коды и высоты по листу выводов сантехники.
4. Облицовка — по сетке швов 2 мм, раскладка от оси стены (треугольник у пола), целые ряды от пола; подрезки — по листу раскладки плитки.
5. Гидроизоляция в 2 слоя, заход на стены 200 мм — до облицовки, с актом скрытых работ и тестом проливом (узел — на листе узлов).

					Проект: Дом 331 м²
	Лист	№ док.	Подпись	Дата	Развёртка стены Б. Санузел мастер (пом. 15)
Дизайнер	Кырлан А.С.			19.10.26	

Стадия	Лист	Листов
П	112	155

выпуск 18.10.2026 № ffc1f29499 · стр. 112 из 155

Развёртка стены В


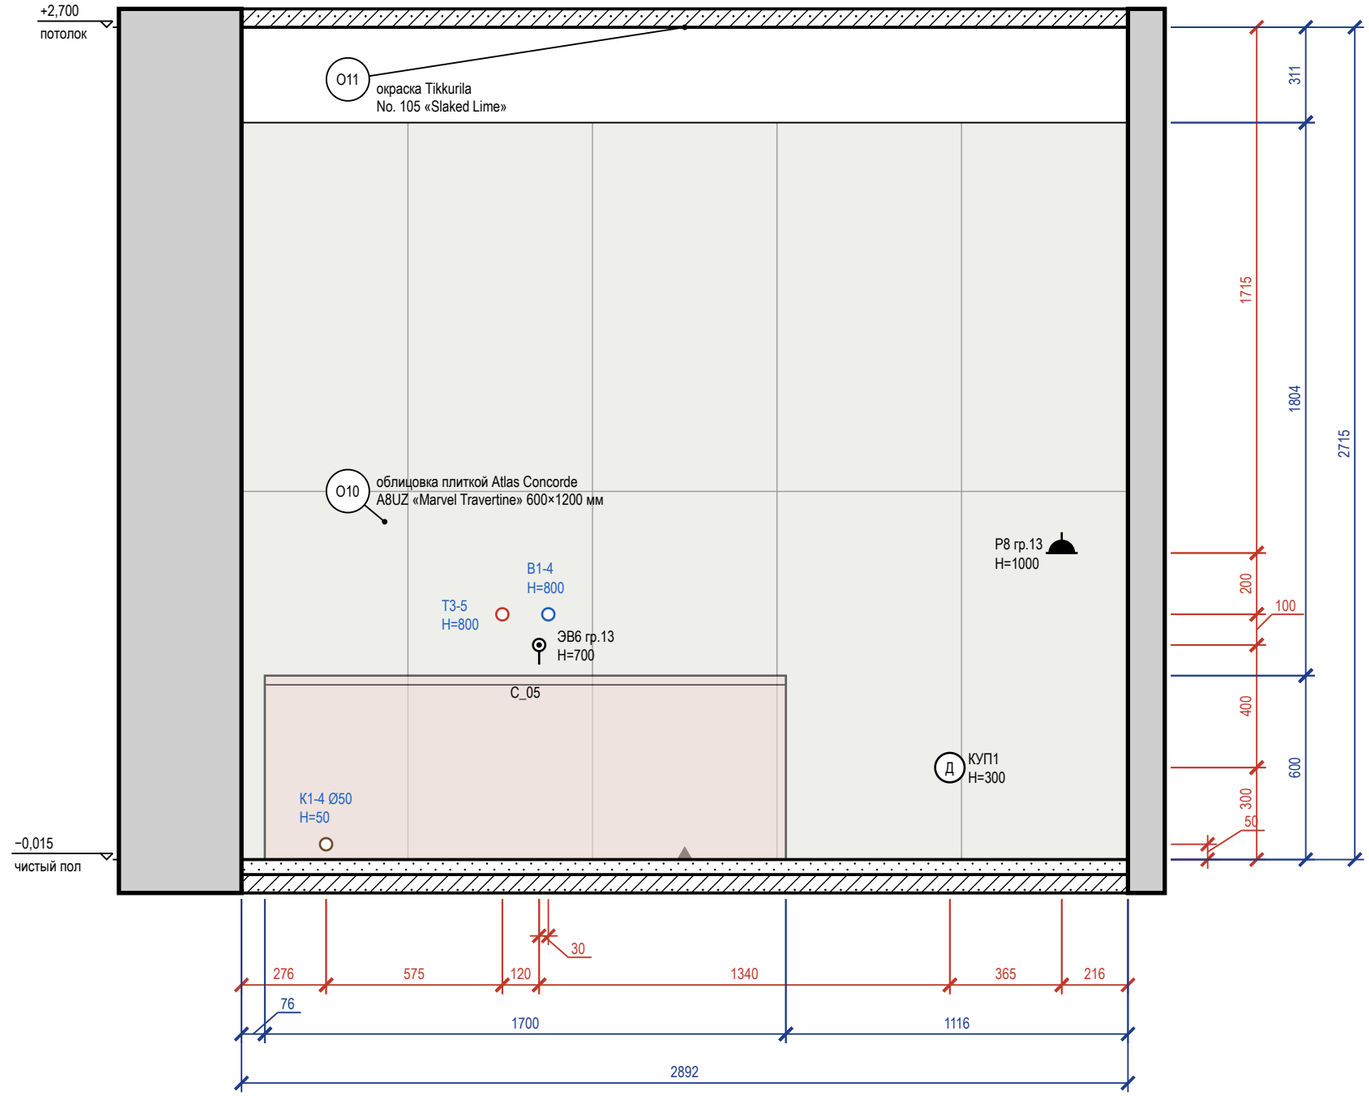


Схема развёрток (М 1:100)

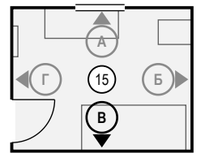

Ведомость отделки (на листе)

Марка	Поверхность	Материал, изделие	Цвет, код	Кол.
О10	стены	облицовка плиткой, Atlas Concorde Marvel Travertine, 600×1200×9 мм, A8UZ, затирка CG2WA	Atlas Concorde A8UZ «Marvel Travertine»	7 м²
О11	потолок	окраска, Tikkurila Luja 7, матовая, подготовка Q3	Little Greene No. 105 «Slaked Lime»	6,9 м²

Примечания

1. Размеры — в мм от чистовых поверхностей стен; условные обозначения и общие указания — лист 2.
2. Схема мебели, приборов и декора не является технической документацией для производства мебели; габариты — по паспортам изделий.
3. Выводы ВК — коды и высоты по листу выводов сантехники.
4. Облицовка — по сетке швов 2 мм, раскладка от оси стены (треугольник у пола), целые ряды от пола; подрезки — по листу раскладки плитки.
5. Гидроизоляция в 2 слоя, заход на стены 200 мм — до облицовки, с актом скрытых работ и тестом проливом (узел — на листе узлов).

					Проект: Дом 331 м²
	Лист	№ док.	Подпись	Дата	Развёртка стены В. Санузел мастер (пом. 15)
Дизайнер	Кырлан А.С.			19.10.26	

Стадия	Лист	Листов
П	113	155

выпуск 18.10.2026 № ffc1f29499 · стр. 113 из 155

Развёртка стены Г


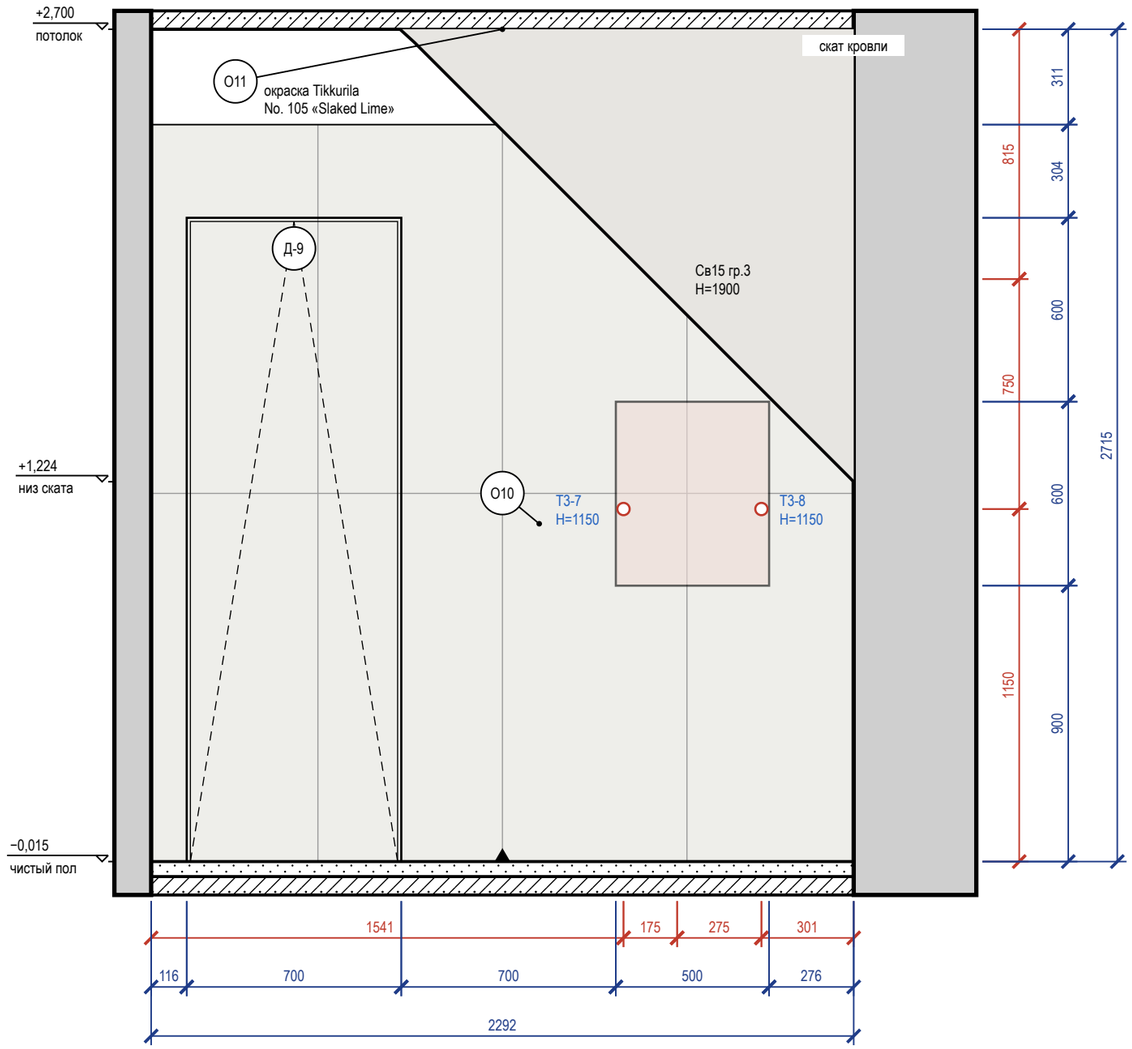


Схема развёрток (М 1:100)

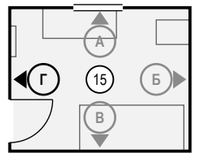

Ведомость отделки (на листе)

Марка	Поверхность	Материал, изделие	Цвет, код	Кол.
О10	стены	облицовка плиткой, Atlas Concorde Marvel Travertine, 600×1200×9 мм, А8UZ, затирка CG2WA	Atlas Concorde A8UZ «Marvel Travertine»	4 м²
О11	потолок	окраска, Tikkurila Luja 7, матовая, подготовка Q3	Little Greene No. 105 «Slaked Lime»	6,9 м²

Визуализация этой стены



Примечания

1. Размеры — в мм от чистовых поверхностей стен; условные обозначения и общие указания — лист 2.
2. Схема мебели, приборов и декора не является технической документацией для производства мебели; габариты — по паспортам изделий.
3. Выводы ВК — коды и высоты по листу выводов сантехники.
4. Облицовка — по сетке швов 2 мм, раскладка от оси стены (треугольник у пола), целые ряды от пола; подрезки — по листу раскладки плитки.
5. Гидроизоляция в 2 слоя, заход на стены 200 мм — до облицовки, с актом скрытых работ и тестом проливом (узел — на листе узлов).
6. Двери скрытого монтажа — полотно в плоскости стены, отделка стены по полотну, плинтус прерывается у короба (узел — на листе узлов).

					Проект: Дом 331 м²
	Лист	№ док.	Подпись	Дата	Развёртка стены Г. Санузел мастер (пом. 15)
Дизайнер	Кырлан А.С.			19.10.26	

Стадия	Лист	Листов
П	114	155

выпуск 18.10.2026 № ffc1f29499 · стр. 114 из 155



					Проект: Дом 331 м²
	Лист	№ док.	Подпись	Дата	Визуализация: Спальня 2
Дизайнер	Кырлан А.С.			19.10.26	

Стадия	Лист	Листов
П	115	155

выпуск 18.10.2026 № ffc1f29499 · стр. 115 из 155



					Проект: Дом 331 м²
	Лист	№ док.	Подпись	Дата	Визуализация: Спальня 2
Дизайнер	Кырлан А.С.			19.10.26	

Стадия	Лист	Листов
П	116	155

выпуск 18.10.2026 № ffc1f29499 · стр. 116 из 155

Развёртка стены А


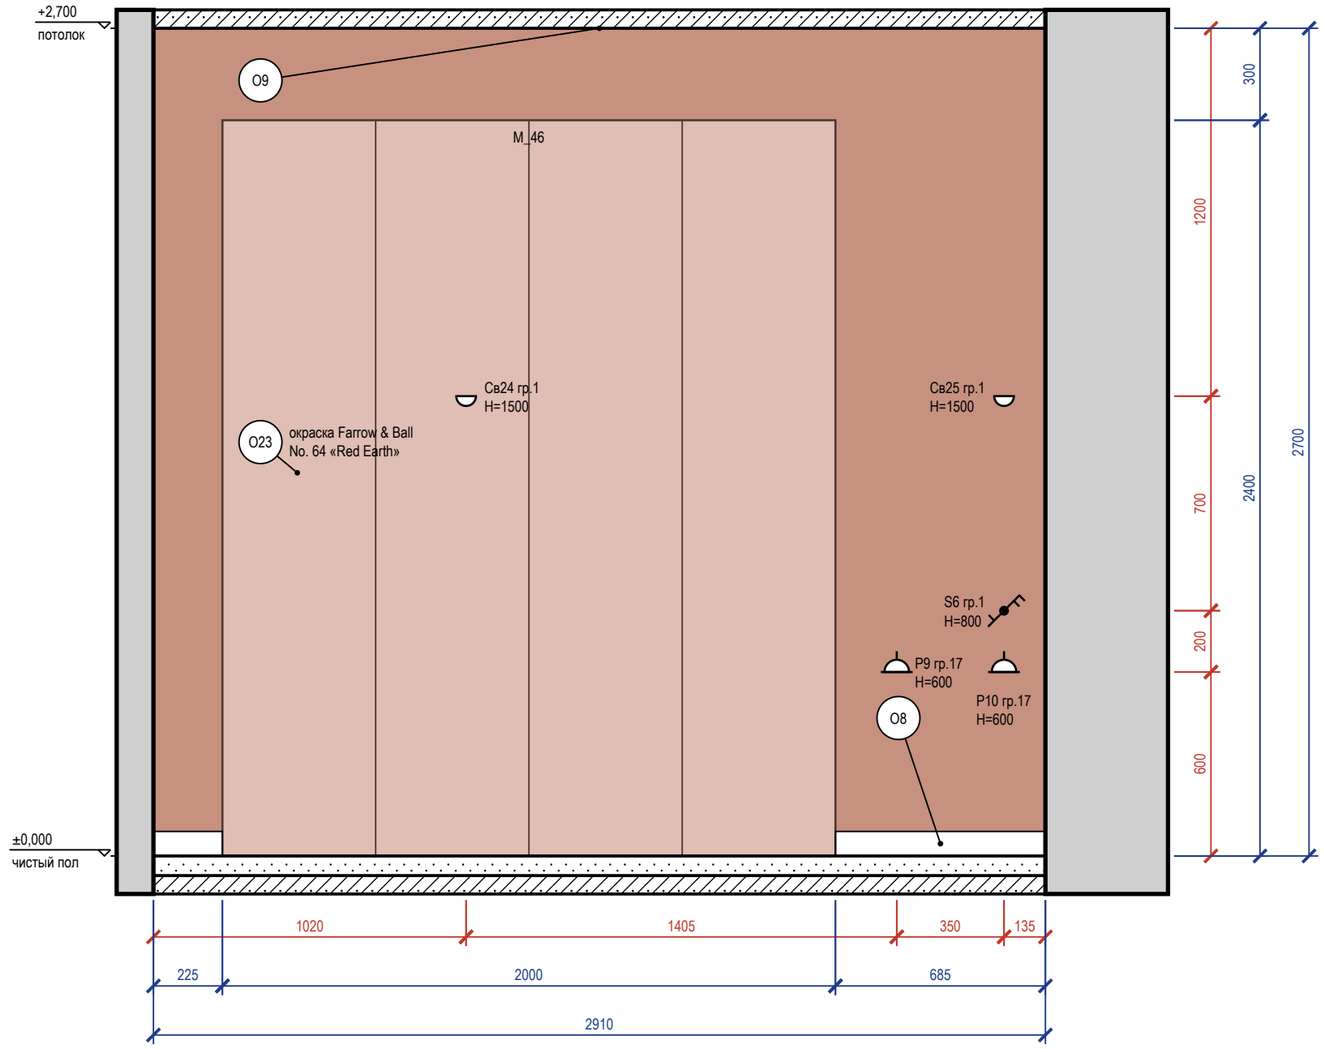


Схема развёрток (М 1:100)

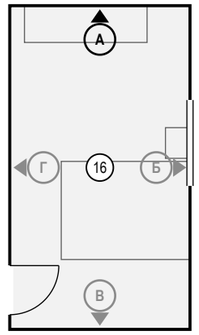

Ведомость отделки (на листе)


Марка	Поверхность	Материал, изделие	Цвет, код	Кол.
О8	плинтус	плинтус МДФ, h 80 мм, аналог: плинтус МДФ под покраску 80×16	Farrow & Ball No. 226 «Joa's White»	0,9 м
О9	потолок	окраска, Tikkurila Anti-Reflex 2, глубокоматовая, подготовка Q3	Little Greene No. 105 «Slaked Lime»	15,5 м²
О23	акцентная стена	окраска, Farrow & Ball Modern Emulsion, матовая, подготовка Q3	Farrow & Ball No. 64 «Red Earth»	7,9 м²

Визуализация этой стены — лист 115



4 **Короб стояков К1-1 с люком и звукоизоляцией (М 1:20)**

Узел 4 — лист С3

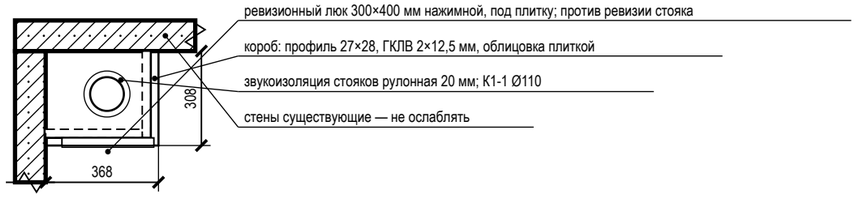

Примечания

1. Размеры — в мм от чистовых поверхностей стен; условные обозначения и общие указания — лист 2.

	Лист	№ док.	Подпись	Дата	Проект: Дом 331 м²
Дизайнер	Кырлан А.С.			19.10.26	Развёртка стены А. Спальня 2 (пом. 16)

Стадия	Лист	Листов
П	117	155

выпуск 18.10.2026 № ffc1f29499 · стр. 117 из 155

Развёртка стены Б


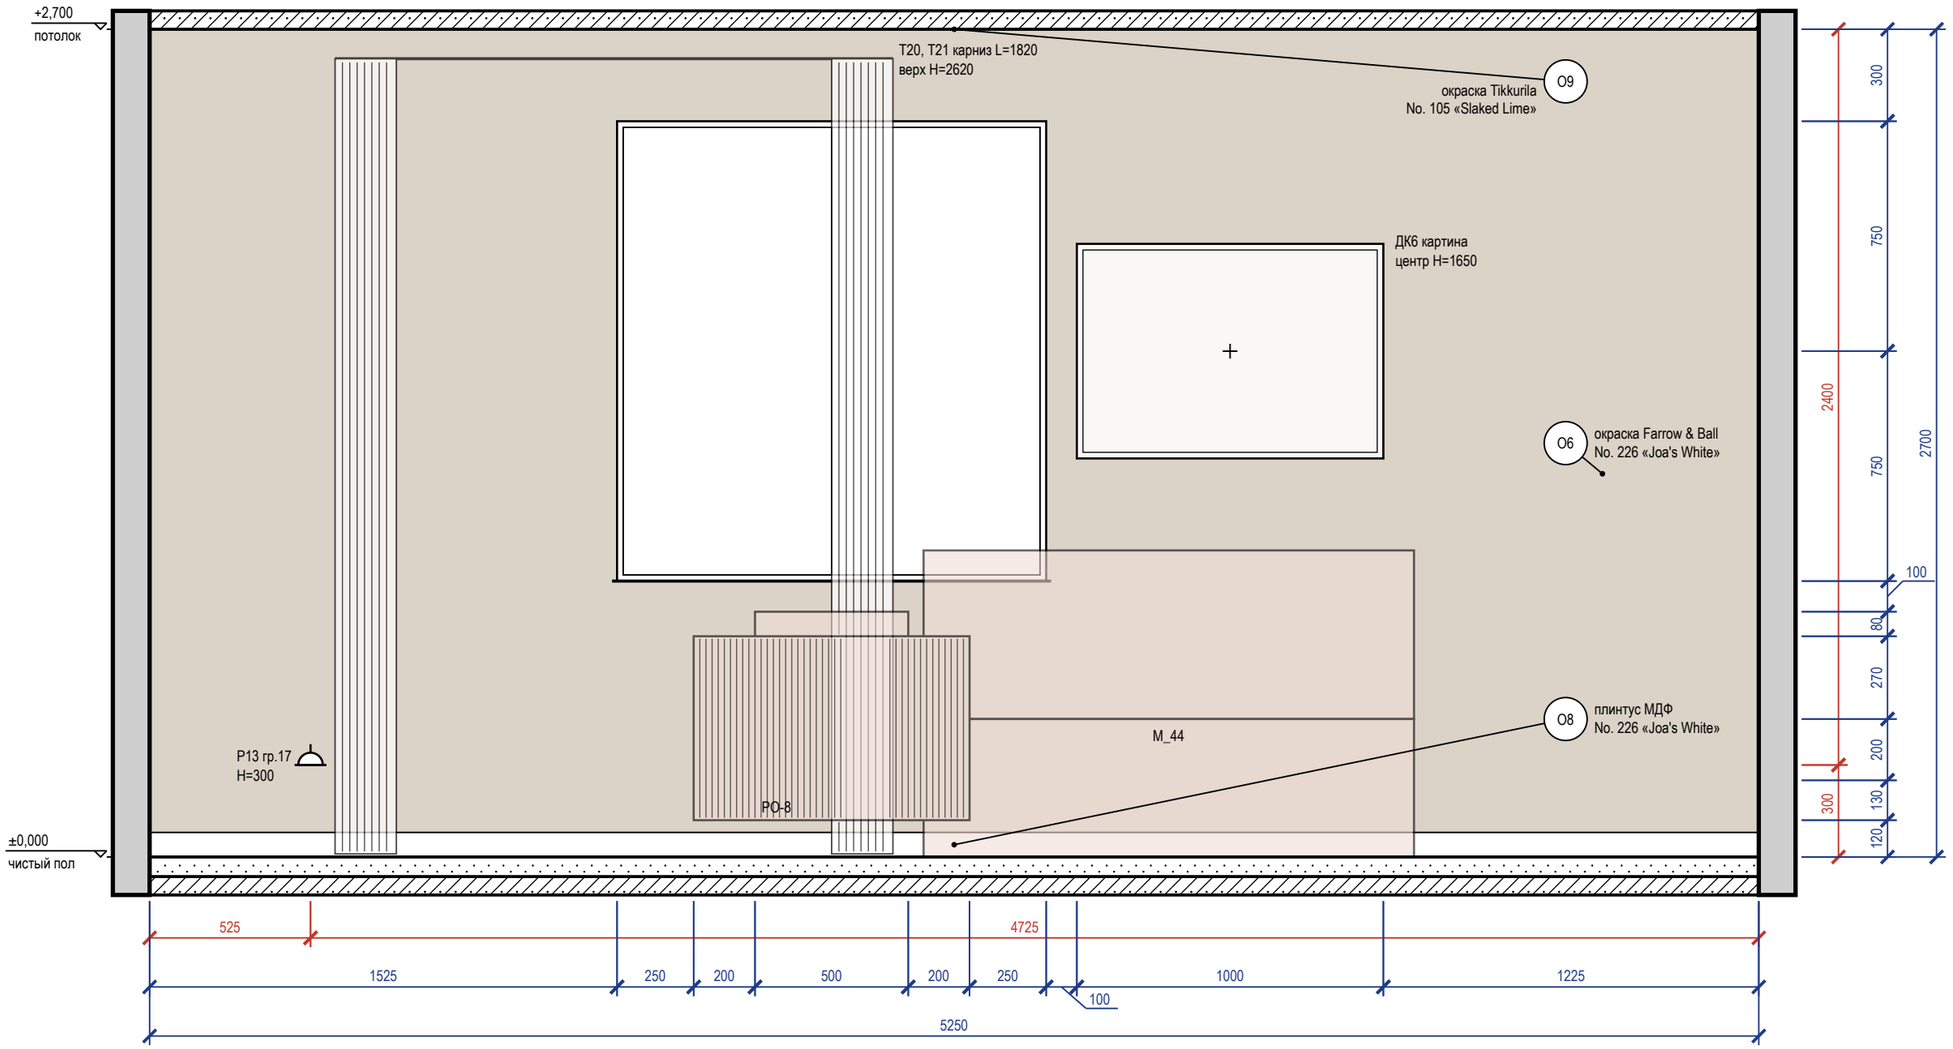



Схема развёрток (М 1:100)

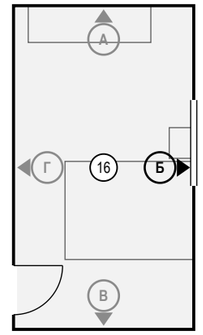

Ведомость отделки (на листе)

Марка	Поверхность	Материал, изделие	Цвет, код	Кол.
О6	стены	окраска, Farrow & Ball Modern Emulsion, матовая, подготовка Q3	Farrow & Ball No. 226 «Joa's White»	12,1 м²
О8	плинтус	плинтус МДФ, h 80 мм, аналог: плинтус МДФ под покраску 80×16	Farrow & Ball No. 226 «Joa's White»	5,3 м
О9	потолок	окраска, Tikkurila Anti-Reflex 2, глубокоматовая, подготовка Q3	Little Greene No. 105 «Slaked Lime»	15,5 м²

Визуализация этой стены

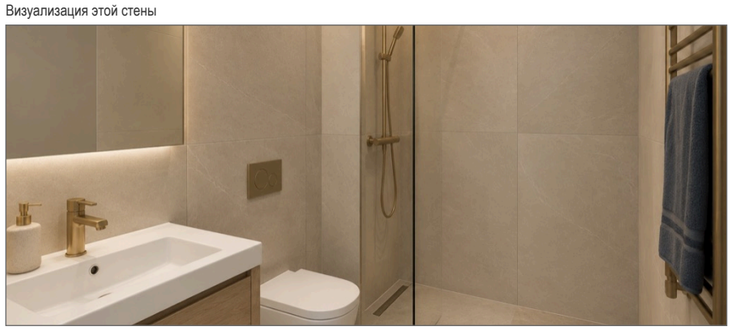

Примечания

1. Размеры — в мм от чистовых поверхностей стен; условные обозначения и общие указания — лист 2.
2. Картины и зеркала крепить к основанию по паспорту изделия (закладные и анкеры — в перечне скрытых работ); крест — ось центра предмета.
3. Карнизы (шины) — по ведомости текстиля декоратора; длина L и верх H — по развёртке, крепление — до окраски потолка.
4. Линии узора (швы плитки, складки штор, рёбра радиаторов) прерываются у знаков и выносок — просвет между линиями не менее 0,7 мм.

	Лист	№ док.	Подпись	Дата
Дизайнер	Кырлан А.С.			19.10.26

Проект: Дом 331 м²

Развёртка стены Б. Спальня 2 (пом. 16)

Стадия	Лист	Листов
П	118	155

выпуск 18.10.2026 № ffc1f29499 · стр. 118 из 155

Развёртка стены В


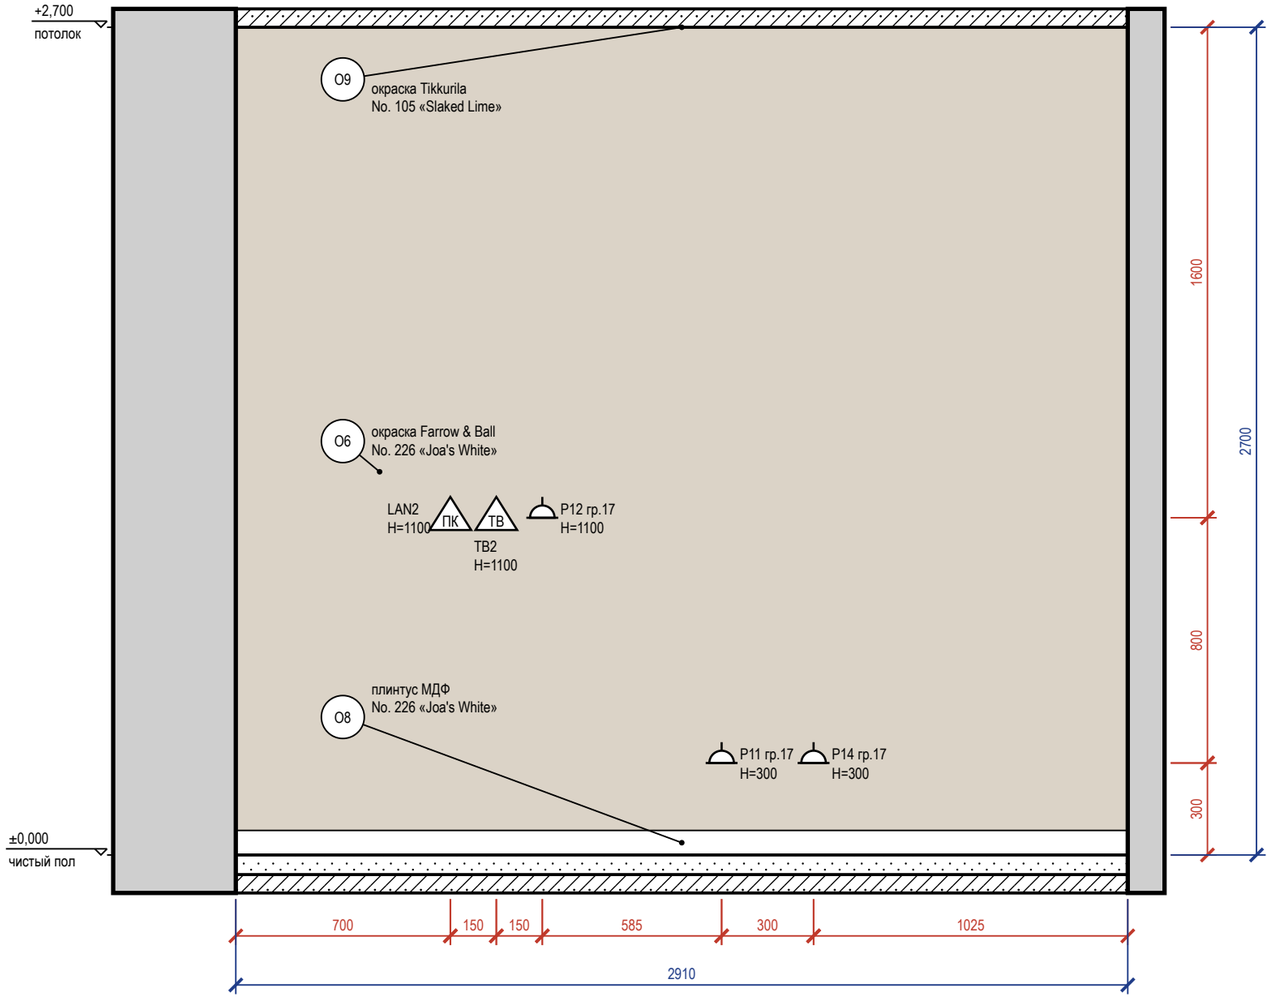


Схема развёрток (М 1:100)

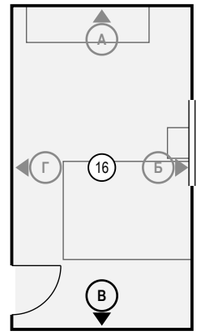

Ведомость отделки (на листе)

Марка	Поверхность	Материал, изделие	Цвет, код	Кол.
О6	стены	окраска, Farrow & Ball Modern Emulsion, матовая, подготовка Q3	Farrow & Ball No. 226 «Joa's White»	7,9 м²
О8	плинтус	плинтус МДФ, h 80 мм, аналог: плинтус МДФ под покраску 80×16	Farrow & Ball No. 226 «Joa's White»	2,9 м
О9	потолок	окраска, Tikkurila Anti-Reflex 2, глубокоматовая, подготовка Q3	Little Greene No. 105 «Slaked Lime»	15,5 м²

Примечания

1. Размеры — в мм от чистовых поверхностей стен; условные обозначения и общие указания — лист 2.

					Проект: Дом 331 м²
	Лист	№ док.	Подпись	Дата	Развёртка стены В. Спальня 2 (пом. 16)
Дизайнер	Кырлан А.С.			19.10.26	

Стадия	Лист	Листов
П	119	155

выпуск 18.10.2026 № ffc1f29499 · стр. 119 из 155

Развёртка стены Г


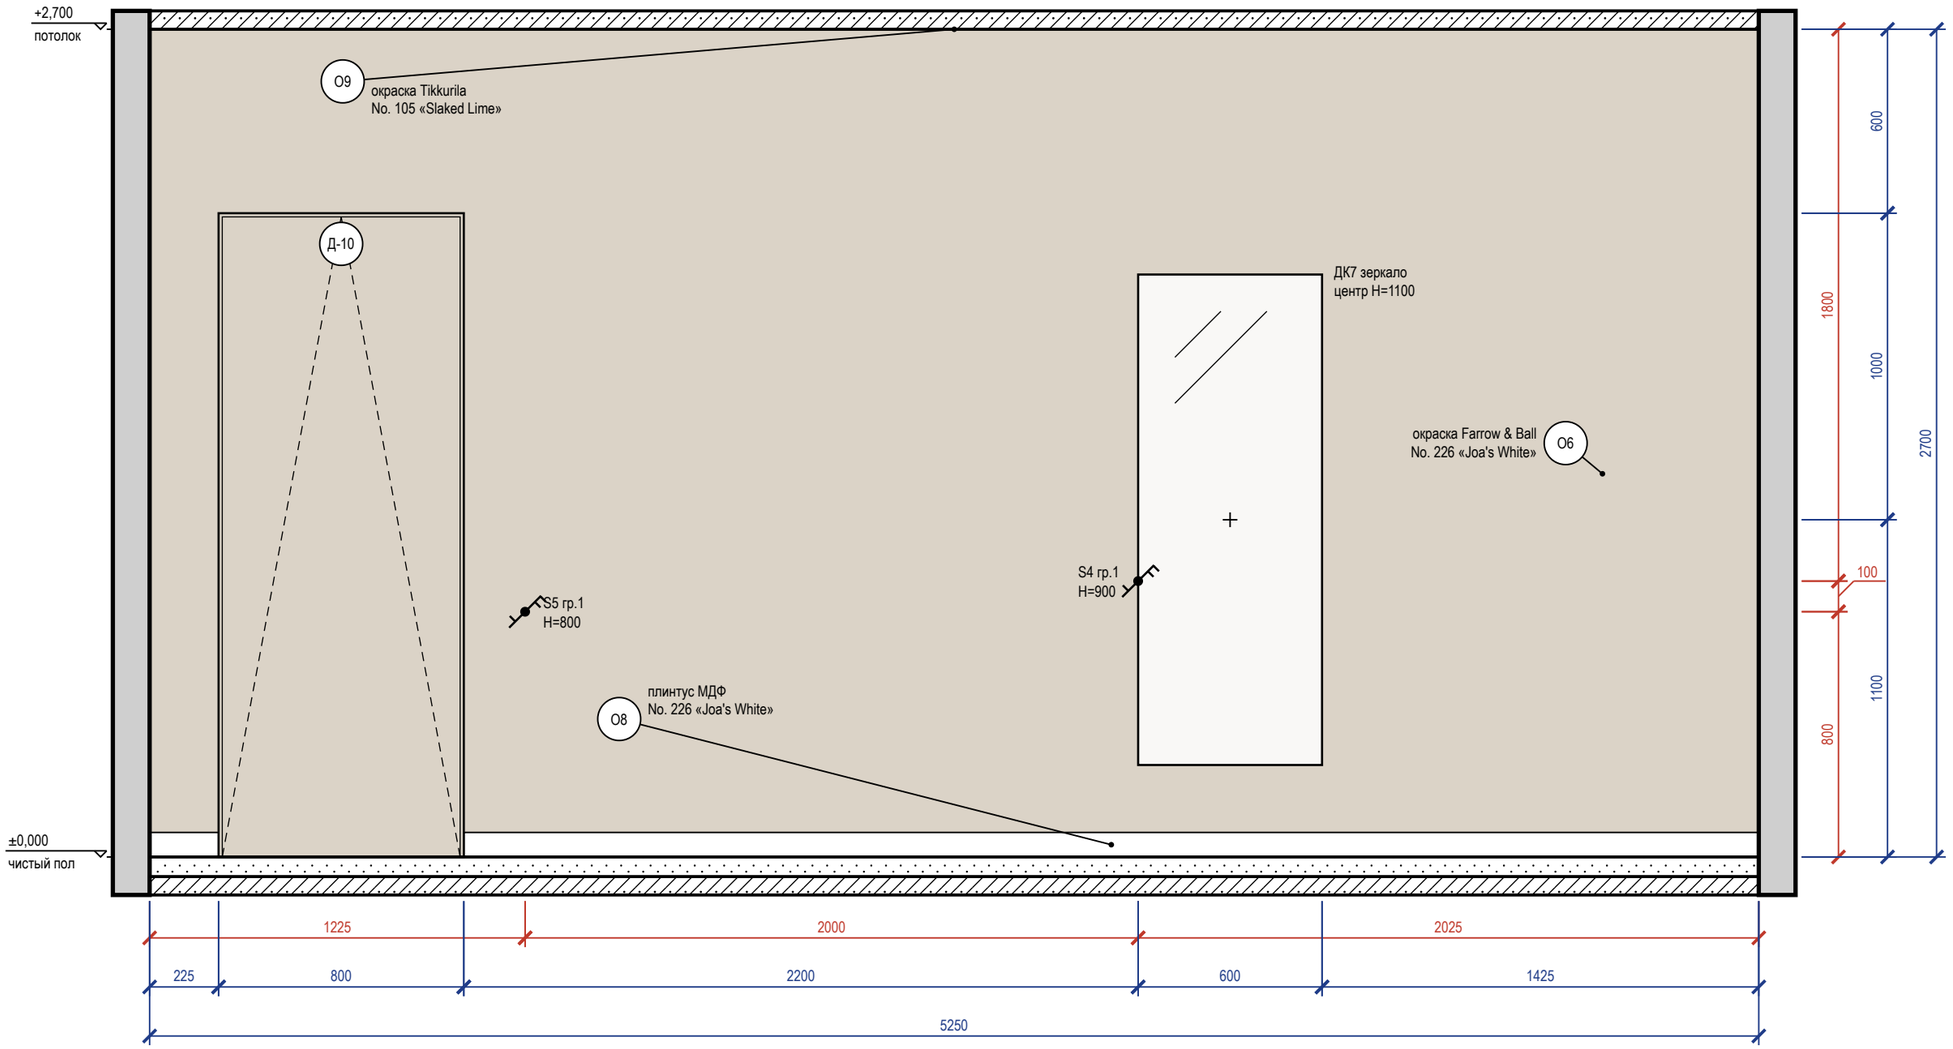


Схема развёрток (М 1:100)

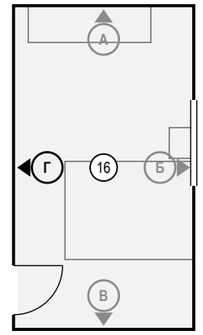

Ведомость отделки (на листе)

Марка	Поверхность	Материал, изделие	Цвет, код	Кол.
О6	стены	окраска, Farrow & Ball Modern Emulsion, матовая, подготовка Q3	Farrow & Ball No. 226 «Joa's White»	12,5 м²
О8	плинтус	плинтус МДФ, h 80 мм, аналог: плинтус МДФ под покраску 80×16	Farrow & Ball No. 226 «Joa's White»	4,5 м
О9	потолок	окраска, Tikkurila Anti-Reflex 2, глубокоматовая, подготовка Q3	Little Greene No. 105 «Slaked Lime»	15,5 м²

Примечания

1. Размеры — в мм от чистовых поверхностей стен; условные обозначения и общие указания — лист 2.
2. Картины и зеркала крепить к основанию по паспорту изделия (закладные и анкеры — в перечне скрытых работ); крест — ось центра предмета.
3. Двери скрытого монтажа — полотно в плоскости стены, отделка стены по полотну, плинтус прерывается у короба (узел — на листе узлов).

	Лист	№ док.	Подпись	Дата
Дизайнер	Кырлан А.С.			19.10.26

Проект: Дом 331 м²

Развёртка стены Г. Спальня 2 (пом. 16)

Стадия	Лист	Листов
П	120	155

выпуск 18.10.2026 № ffc1f29499 · стр. 120 из 155



					Проект: Дом 331 м²	
	Лист	№ док.	Подпись	Дата		
Дизайнер	Кырлан А.С.			19.10.26	Визуализация: Холл мансарды	Стадия / Лист / Листов
						П / 121 / 155

выпуск 18.10.2026 № ffc1f29499 · стр. 121 из 155

Развёртка стены А


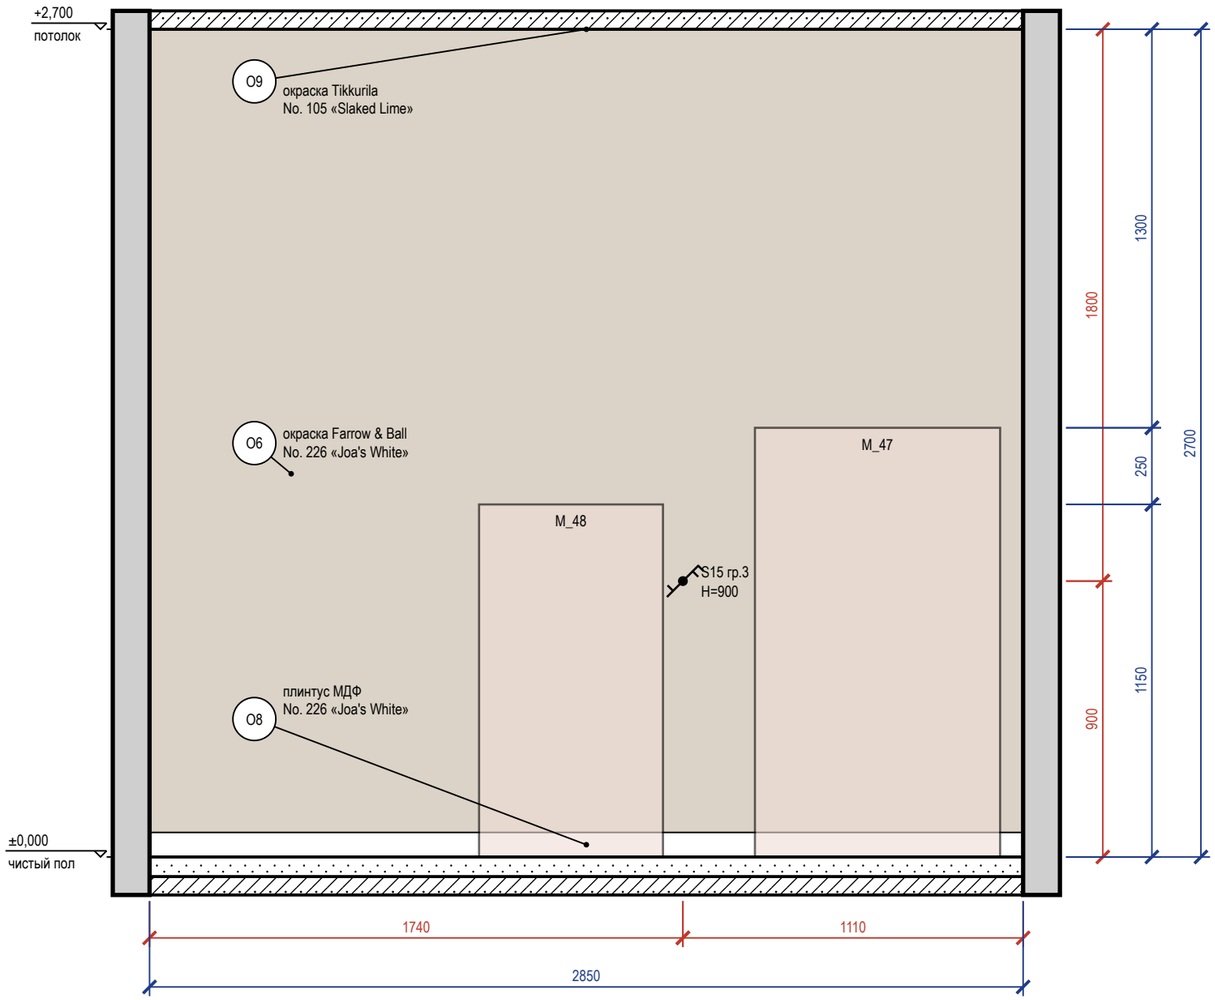


Схема развёрток (М 1:100)

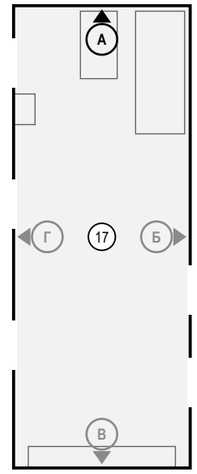

Ведомость отделки (на листе)

Марка	Поверхность	Материал, изделие	Цвет, код	Кол.
О6	стены	окраска, Farrow & Ball Modern Emulsion, матовая, подготовка Q3	Farrow & Ball No. 226 «Joa's White»	7,7 м²
О8	плинтус	плинтус МДФ, h 80 мм, аналог: плинтус МДФ под покраску 80×16	Farrow & Ball No. 226 «Joa's White»	2,9 м
О9	потолок	окраска, Tikkurila Anti-Reflex 2, глубокоматовая, подготовка Q3	Little Greene No. 105 «Slaked Lime»	21,7 м²

Примечания

1. Размеры — в мм от чистовых поверхностей стен; условные обозначения и общие указания — лист 2.

					Проект: Дом 331 м²
	Лист	№ док.	Подпись	Дата	Развёртка стены А. Холл мансарды (пом. 17)
Дизайнер	Кырлан А.С.			19.10.26	

Стадия	Лист	Листов
П	122	155

выпуск 18.10.2026 № ffc1f29499 · стр. 122 из 155

Развёртка стены Б


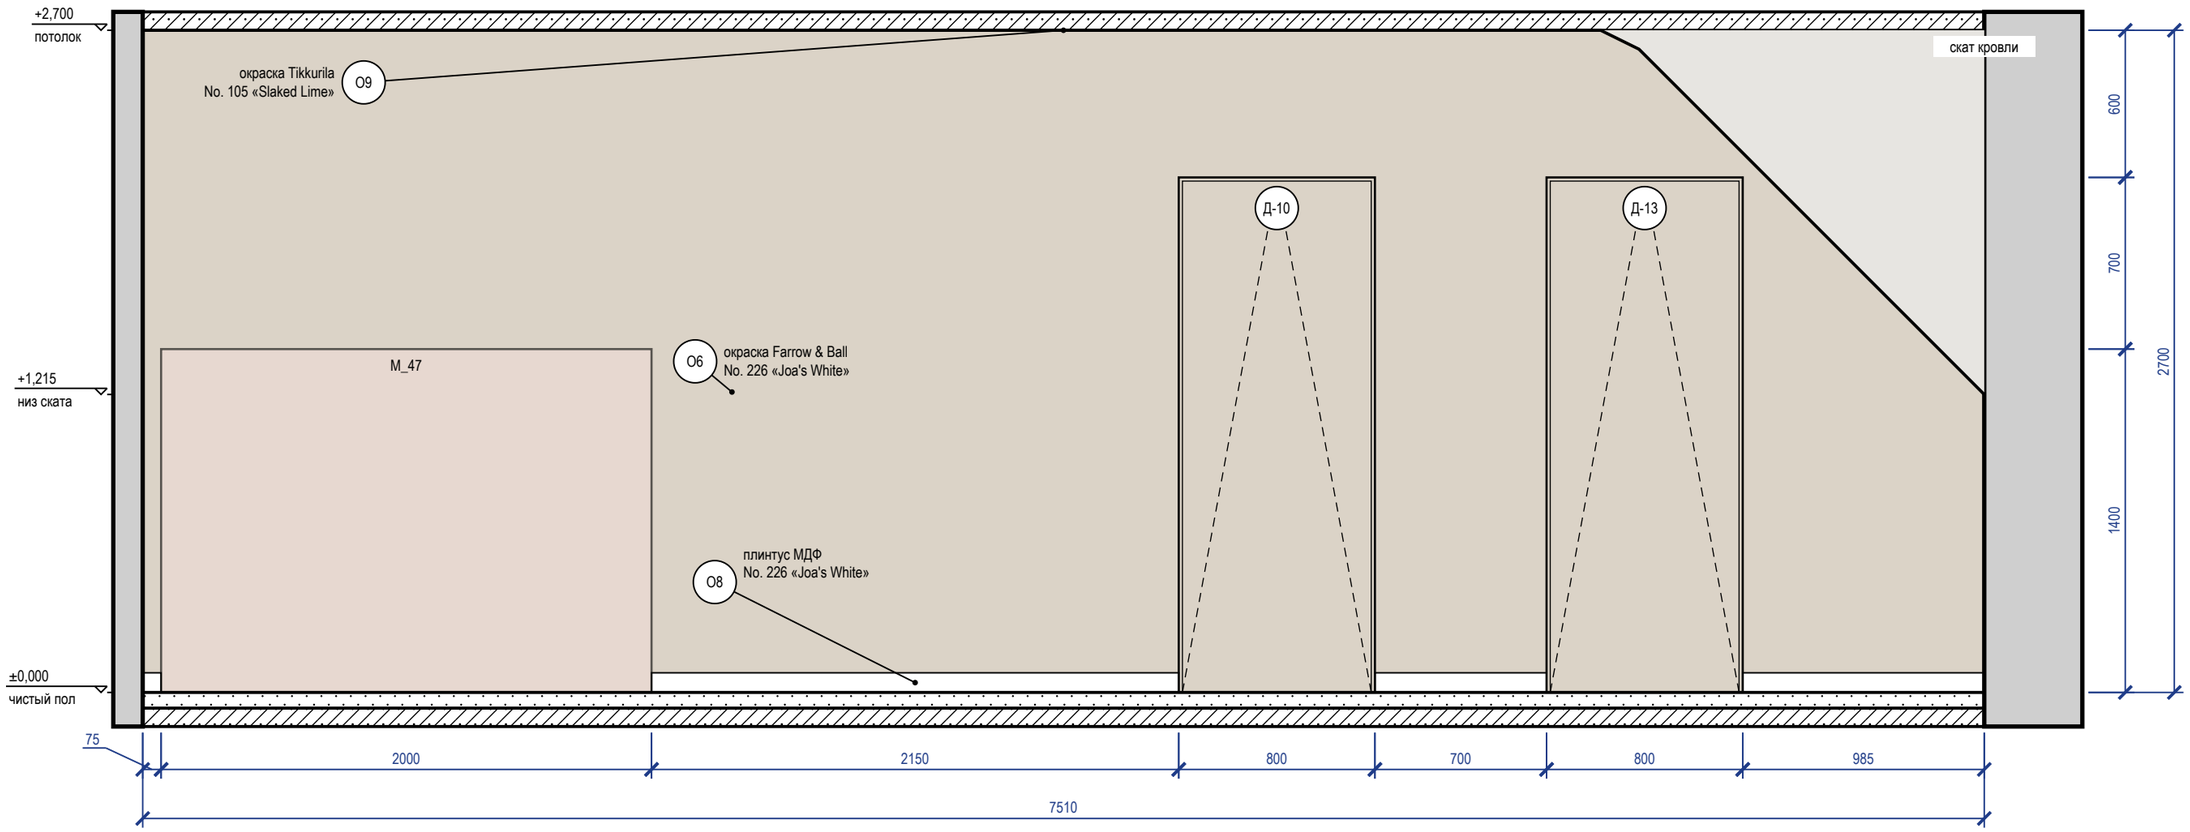


Схема развёрток (М 1:100)

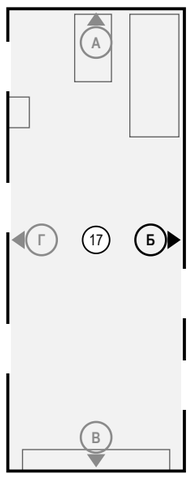

Ведомость отделки (на листе)

Марка	Поверхность	Материал, изделие	Цвет, код	Кол.
О6	стены	окраска, Farrow & Ball Modern Emulsion, матовая, подготовка Q3	Farrow & Ball No. 226 «Joa's White»	16,9 м²
О8	плинтус	плинтус МДФ, h 80 мм, аналог: плинтус МДФ под покраску 80×16	Farrow & Ball No. 226 «Joa's White»	3,9 м
О9	потолок	окраска, Tikkurila Anti-Reflex 2, глубокоматовая, подготовка Q3	Little Greene No. 105 «Slaked Lime»	21,7 м²

Примечания

1. Размеры — в мм от чистовых поверхностей стен; условные обозначения и общие указания — лист 2.
2. Двери скрытого монтажа — полотно в плоскости стены, отделка стены по полотну, плинтус прерывается у короба (узел — на листе узлов).

					Проект: Дом 331 м²
	Лист	№ док.	Подпись	Дата	Развёртка стены Б. Холл мансарды (пом. 17)
Дизайнер	Кырлан А.С.			19.10.26	

Стадия	Лист	Листов
П	123	155

выпуск 18.10.2026 · ffc1f29499 · стр. 123 из 155

Развёртка стены В


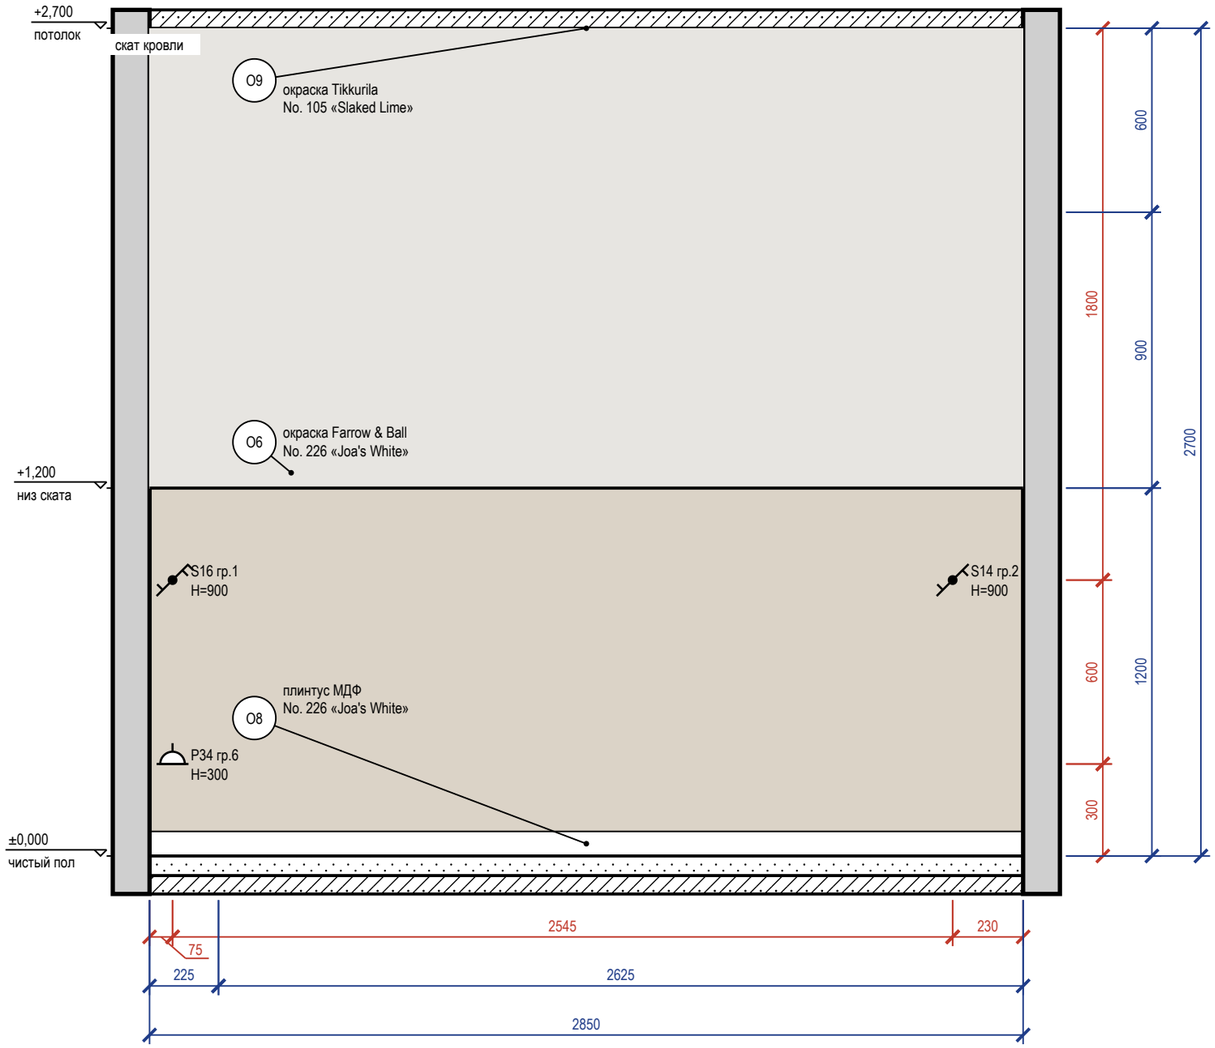


Схема развёрток (М 1:100)

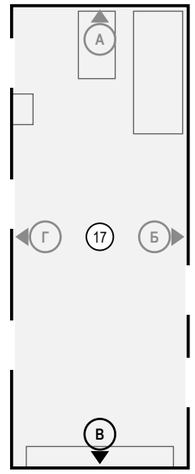

Ведомость отделки (на листе)

Марка	Поверхность	Материал, изделие	Цвет, код	Кол.
О6	стены	окраска, Farrow & Ball Modern Emulsion, матовая, подготовка Q3	Farrow & Ball No. 226 «Joa's White»	7,7 м²
О8	плинтус	плинтус МДФ, h 80 мм, аналог: плинтус МДФ под покраску 80×16	Farrow & Ball No. 226 «Joa's White»	2,9 м
О9	потолок	окраска, Tikkurila Anti-Reflex 2, глубокоматовая, подготовка Q3	Little Greene No. 105 «Slaked Lime»	21,7 м²

Визуализация этой стены — лист 121



Примечания

1. Размеры — в мм от чистовых поверхностей стен; условные обозначения и общие указания — лист 2.
2. Схема мебели, приборов и декора не является технической документацией для производства мебели; габариты — по паспортам изделий.

	Лист	№ док.	Подпись	Дата
Дизайнер	Кырлан А.С.			19.10.26

Проект: Дом 331 м²

Развёртка стены В. Холл мансарды (пом. 17)

Стадия	Лист	Листов
П	124	155

выпуск 18.10.2026 № ffc1f29499 · стр. 124 из 155

Развёртка стены Г


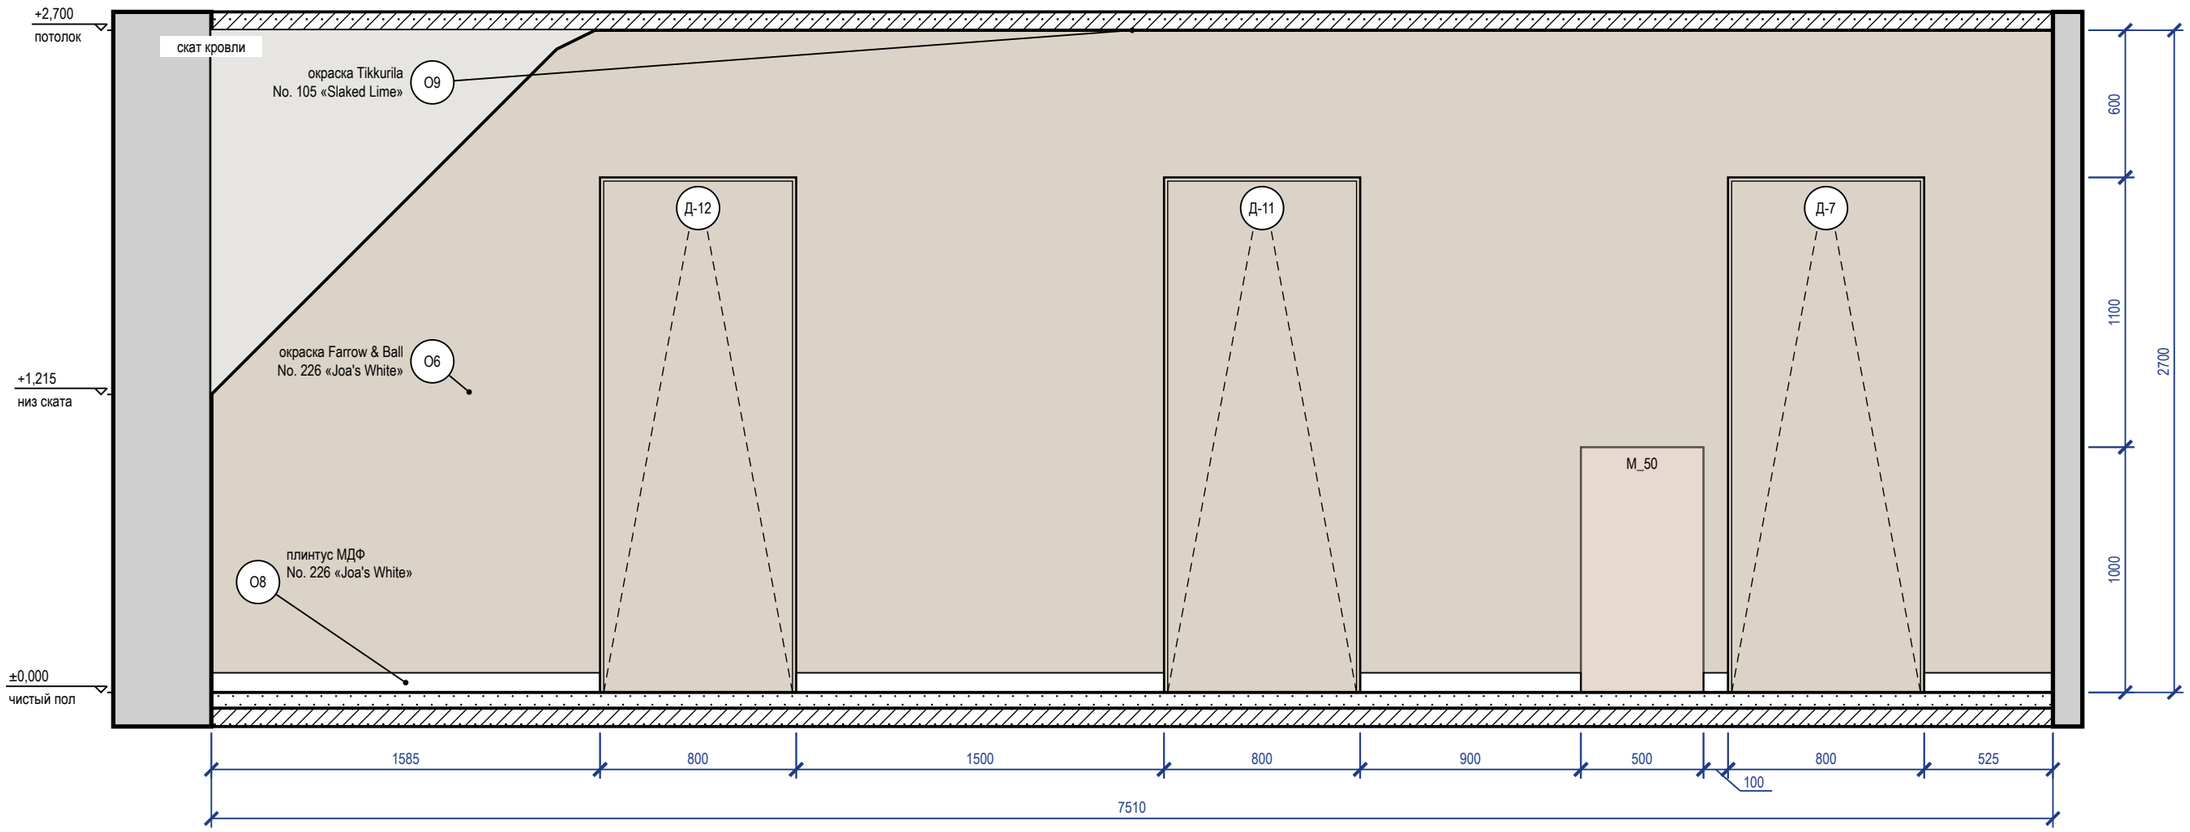


Схема развёрток (М 1:100)

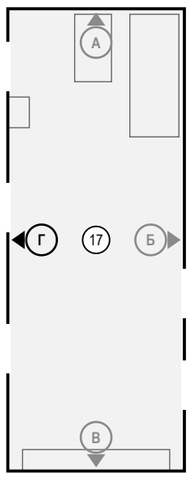

Ведомость отделки (на листе)

Марка	Поверхность	Материал, изделие	Цвет, код	Кол.
О6	стены	окраска, Farrow & Ball Modern Emulsion, матовая, подготовка Q3	Farrow & Ball No. 226 «Joa's White»	15,2 м²
О8	плинтус	плинтус МДФ, h 80 мм, аналог: плинтус МДФ под покраску 80×16	Farrow & Ball No. 226 «Joa's White»	4,6 м
О9	потолок	окраска, Tikkurila Anti-Reflex 2, глубокоматовая, подготовка Q3	Little Greene No. 105 «Slaked Lime»	21,7 м²

Примечания

1. Размеры — в мм от чистовых поверхностей стен; условные обозначения и общие указания — лист 2.
2. Двери скрытого монтажа — полотно в плоскости стены, отделка стены по полотну, плинтус прерывается у короба (узел — на листе узлов).

					Проект: Дом 331 м²
	Лист	№ док.	Подпись	Дата	Развёртка стены Г. Холл мансарды (пом. 17)
Дизайнер	Кырлан А.С.			19.10.26	

Стадия	Лист	Листов
П	125	155

выпуск 18.10.2026 · ffc1f29499 · стр. 125 из 155



					Проект: Дом 331 м²	
	Лист	№ док.	Подпись	Дата	Визуализация: Спальня 3	Стадия / Лист / Листов
Дизайнер	Кырлан А.С.			19.10.26		П / 126 / 155

выпуск 18.10.2026 № ffc1f29499 · стр. 126 из 155



					Проект: Дом 331 м²
	Лист	№ док.	Подпись	Дата	Визуализация: Спальня 3
Дизайнер	Кырлан А.С.			19.10.26	

Стадия	Лист	Листов
П	127	155

выпуск 18.10.2026 № ffc1f29499 · стр. 127 из 155

Развёртка стены А


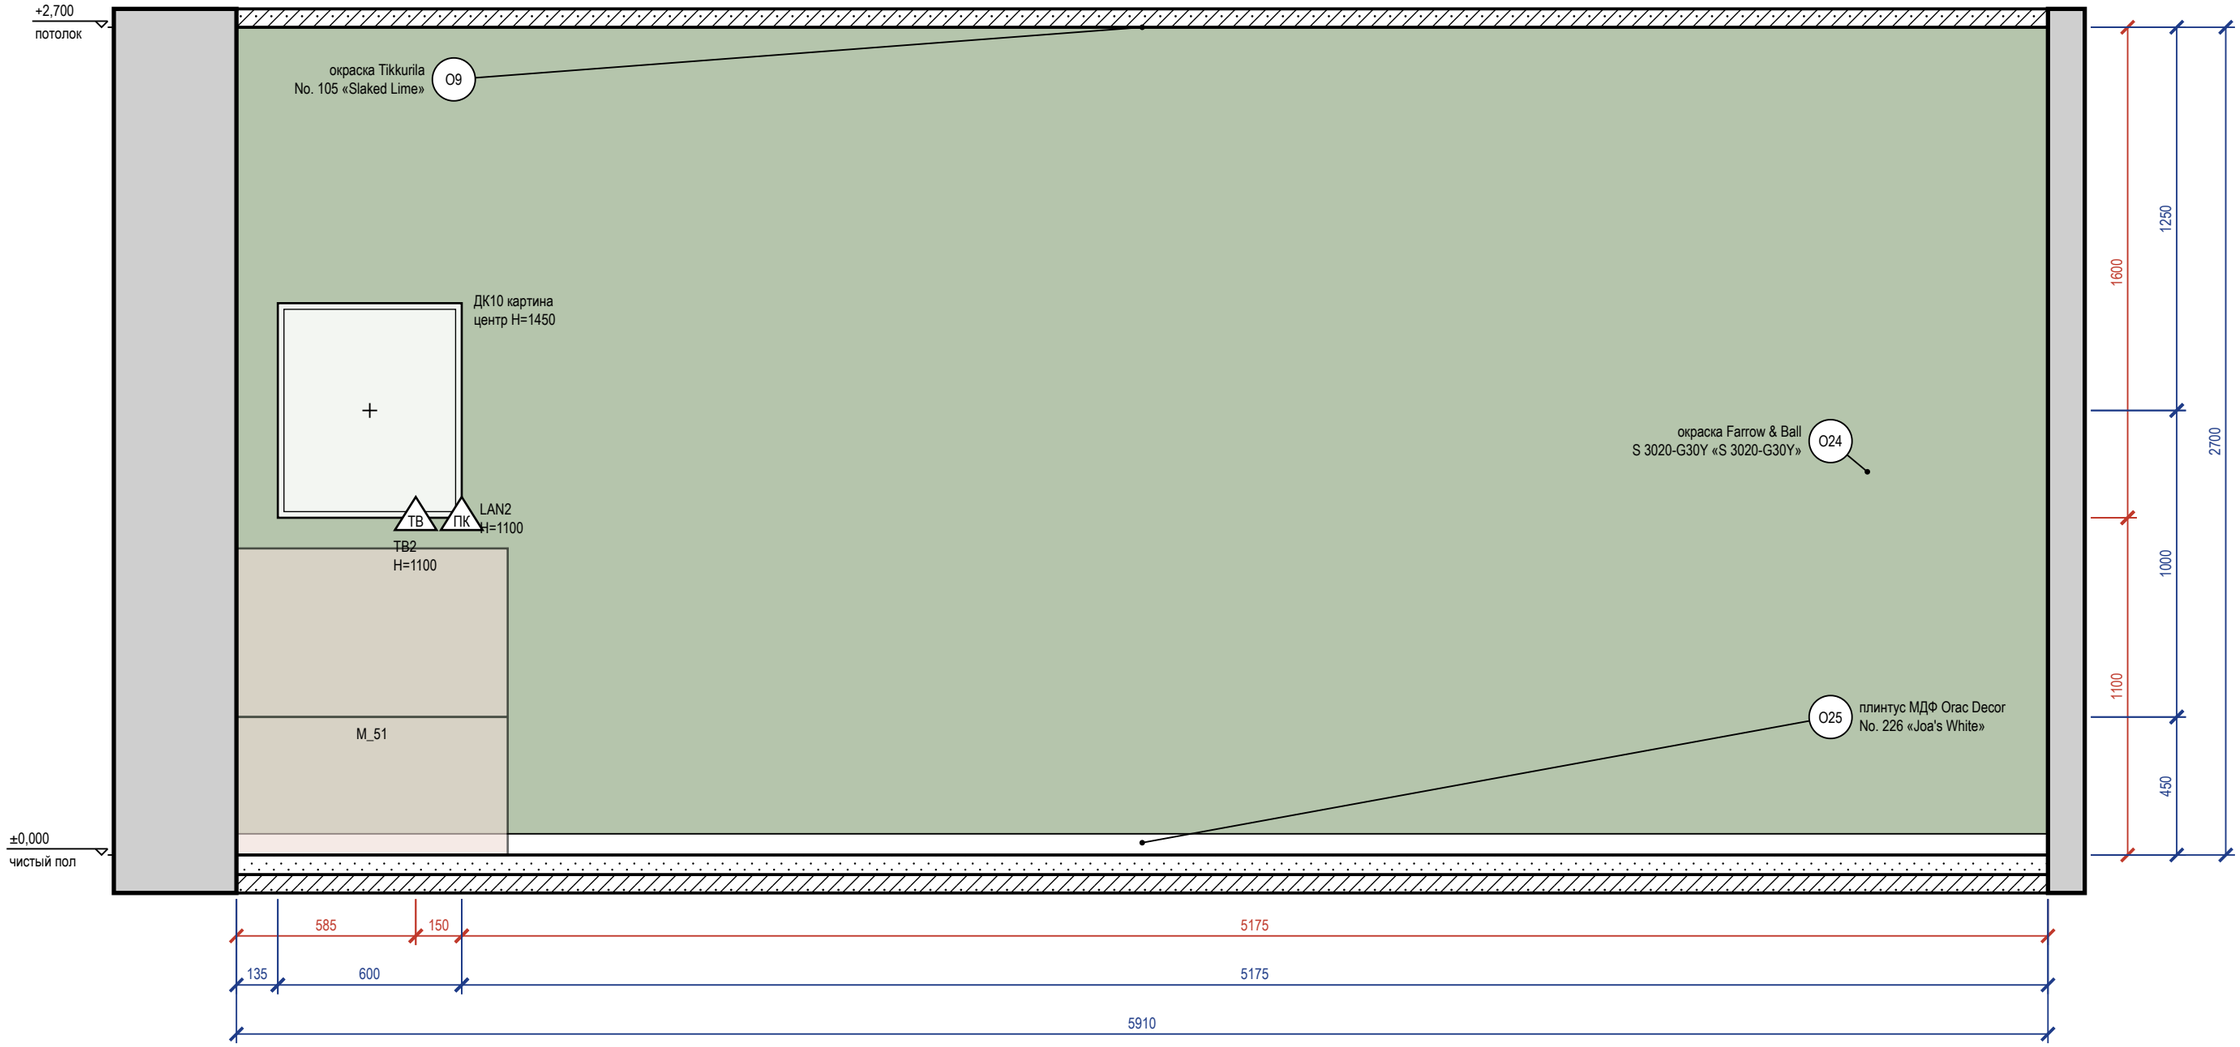


Схема развёрток (М 1:100)

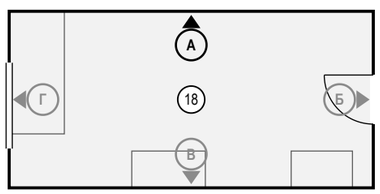

Ведомость отделки (на листе)

Марка	Поверхность	Материал, изделие	Цвет, код	Кол.
O9	потолок	окраска, Tikkurila Anti-Reflex 2, глубокоматовая, подготовка Q3	Little Greene No. 105 «Slaked Lime»	17,1 м²
O24	акцентная стена	окраска, Farrow & Ball Modern Emulsion, матовая, подготовка Q3	NCS S 3020-G30Y «S 3020-G30Y»	16 м²
O25	плинтус	плинтус МДФ, Orac Decor Contour (Luxxus), h 69 мм, SX165	Farrow & Ball No. 226 «Joa's White»	5,9 м

Визуализация этой стены



Примечания

1. Размеры — в мм от чистовых поверхностей стен; условные обозначения и общие указания — лист 2.
2. Картины и зеркала крепить к основанию по паспорту изделия (закладные и анкеры — в перечне скрытых работ); крест — ось центра предмета.

					Проект: Дом 331 м²
	Лист	№ док.	Подпись	Дата	
Дизайнер	Кырлан А.С.			19.10.26	Развёртка стены А. Спальня 3 (пом. 18)

Стадия	Лист	Листов
П	128	155

выпуск 18.10.2026 № ffc1f29499 · стр. 128 из 155

Развёртка стены Б


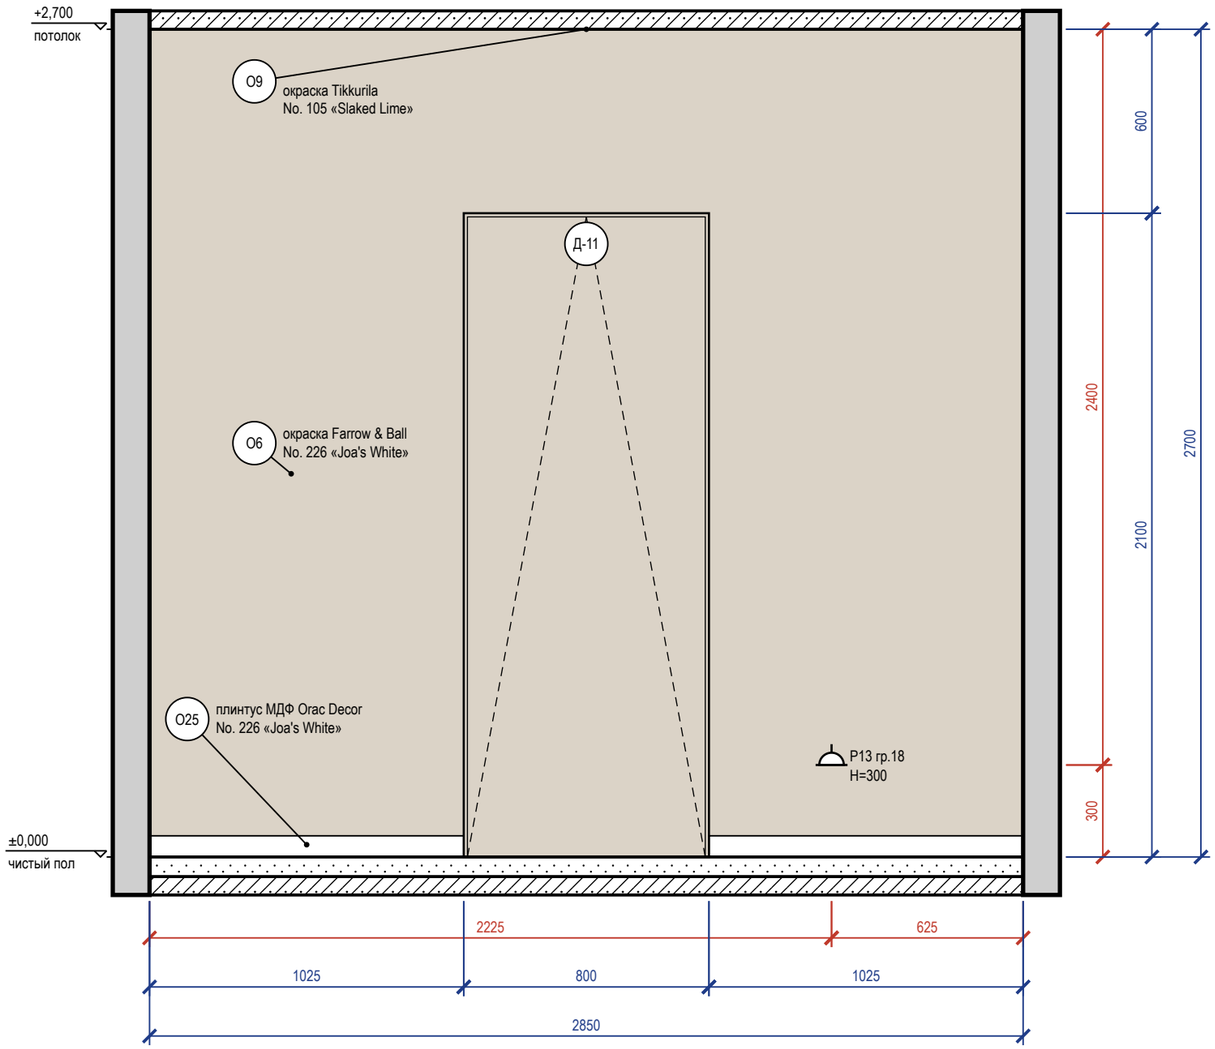


Схема развёрток (М 1:100)

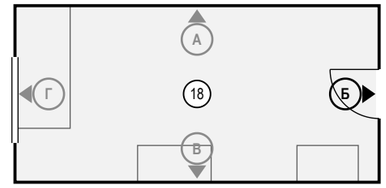

Ведомость отделки (на листе)

Марка	Поверхность	Материал, изделие	Цвет, код	Кол.
О6	стены	окраска, Farrow & Ball Modern Emulsion, матовая, подготовка Q3	Farrow & Ball No. 226 «Joa's White»	6 м²
О9	потолок	окраска, Tikkurila Anti-Reflex 2, глубокоматовая, подготовка Q3	Little Greene No. 105 «Slaked Lime»	17,1 м²
О25	плинтус	плинтус МДФ, Orac Decor Contour (Luxxus), h 69 мм, SX165	Farrow & Ball No. 226 «Joa's White»	2 м

Примечания

1. Размеры — в мм от чистовых поверхностей стен; условные обозначения и общие указания — лист 2.
2. Двери скрытого монтажа — полотно в плоскости стены, отделка стены по полотну, плинтус прерывается у короба (узел — на листе узлов).

					Проект: Дом 331 м²
	Лист	№ док.	Подпись	Дата	Развёртка стены Б. Спальня 3 (пом. 18)
Дизайнер	Кырлан А.С.			19.10.26	

Стадия	Лист	Листов
П	129	155

выпуск 18.10.2026 № ffc1f29499 · стр. 129 из 155

Развёртка стены В


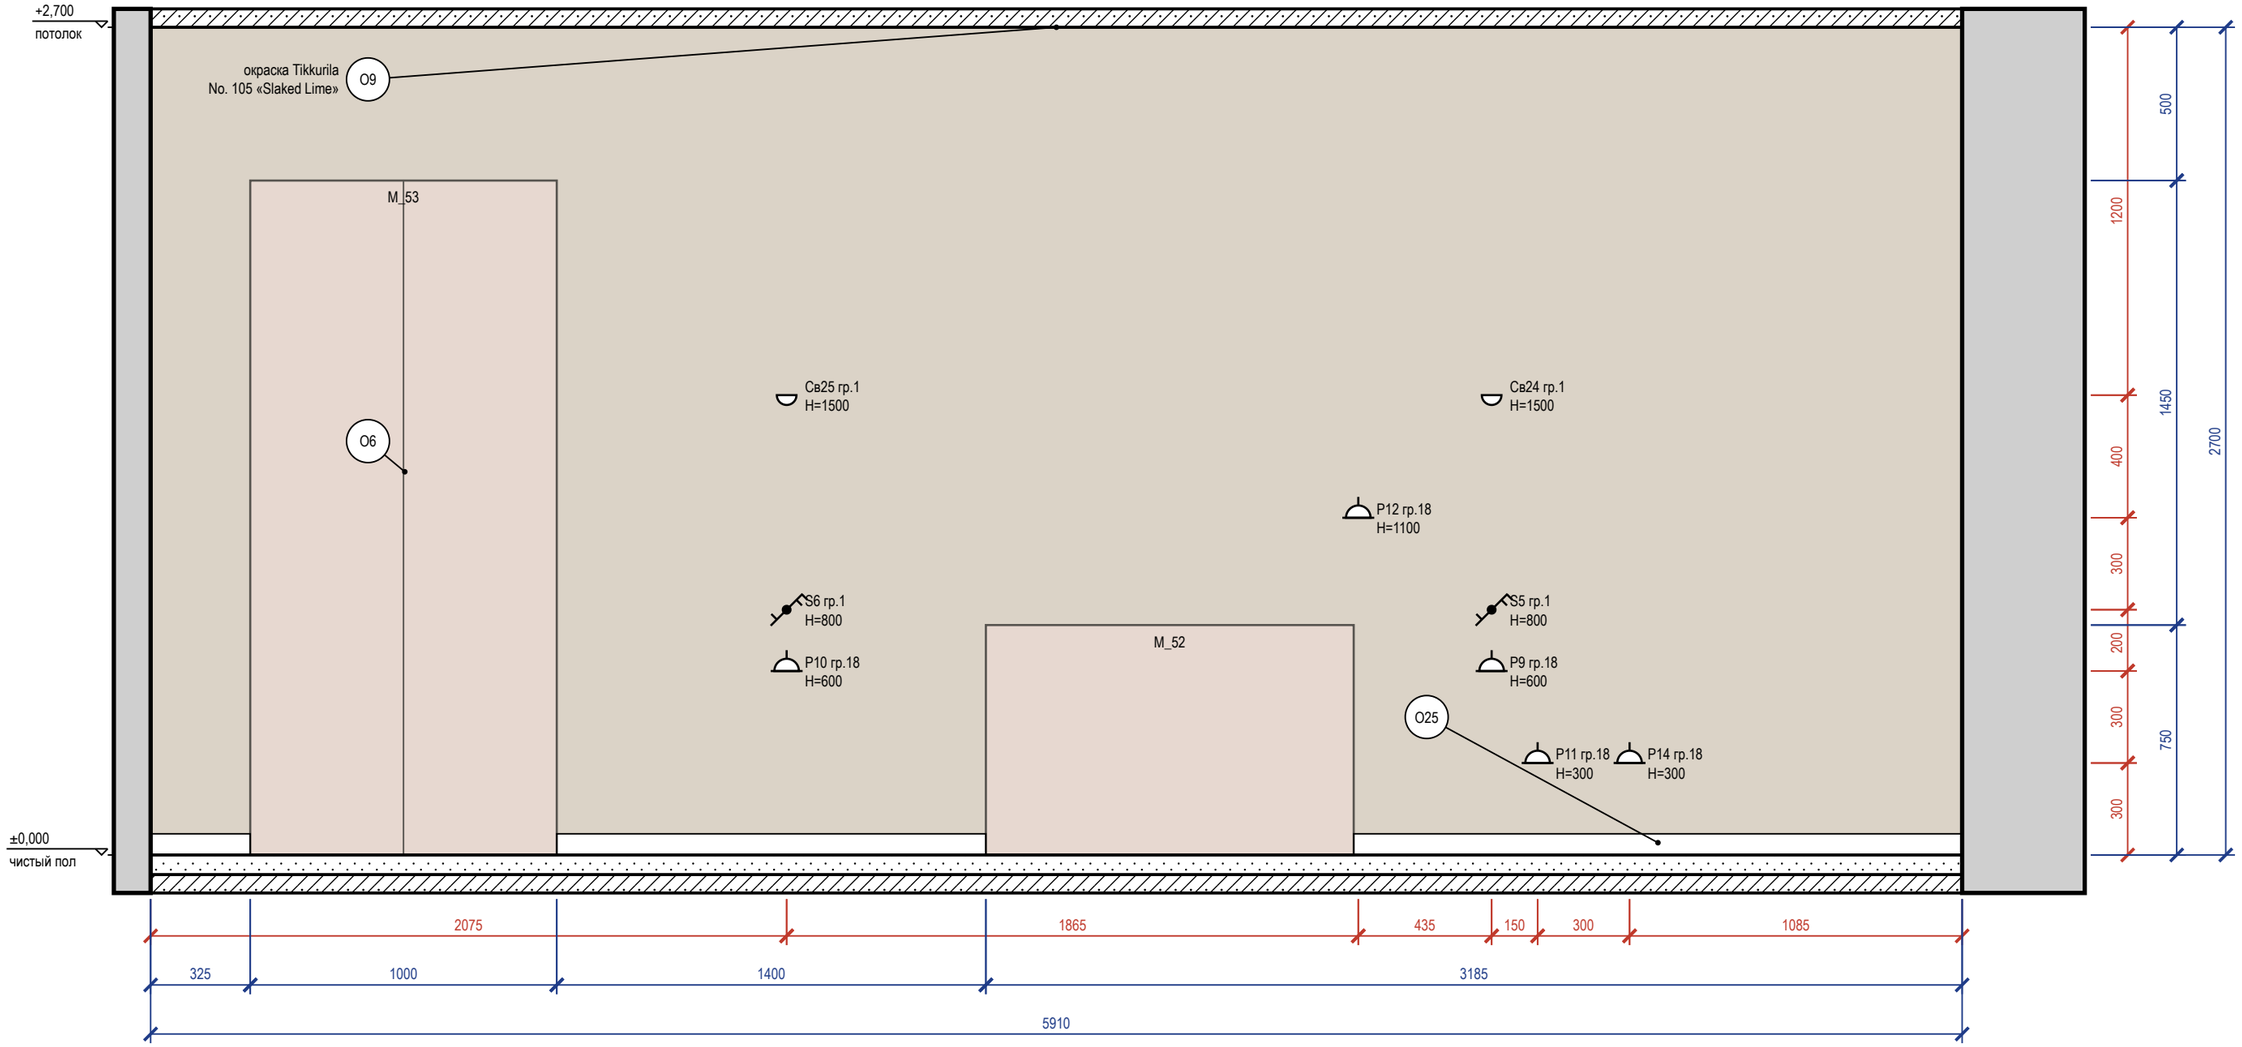



Схема развёрток (М 1:100)

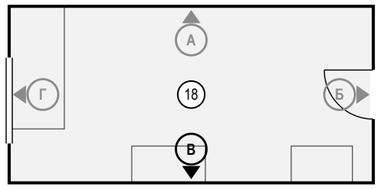

Ведомость отделки (на листе)

Марка	Поверхность	Материал, изделие	Цвет, код	Кол.
О6	стены	окраска, Farrow & Ball Modern Emulsion, матовая, подготовка Q3	Farrow & Ball No. 226 «Joa's White»	16 м²
О9	потолок	окраска, Tikkurila Anti-Reflex 2, глубокоматовая, подготовка Q3	Little Greene No. 105 «Slaked Lime»	17,1 м²
О25	плинтус	плинтус МДФ, Orac Decor Contour (Luxxus), h 69 мм, SX165	Farrow & Ball No. 226 «Joa's White»	3,7 м

Визуализация этой стены — лист 127

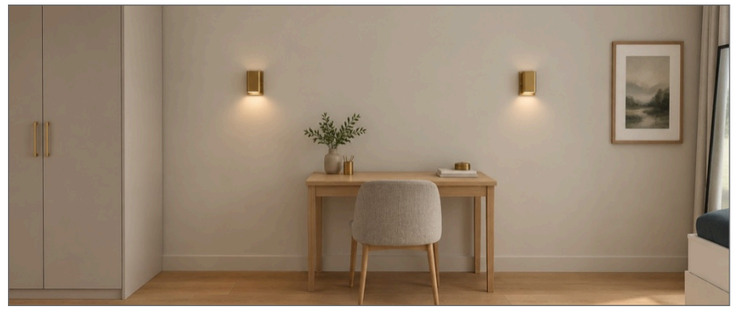

Примечания

1. Размеры — в мм от чистовых поверхностей стен; условные обозначения и общие указания — лист 2.

	Лист	№ док.	Подпись	Дата	Проект: Дом 331 м²
Дизайнер	Кырлан А.С.			19.10.26	Развёртка стены В. Спальня 3 (пом. 18)

Стадия	Лист	Листов
П	130	155

выпуск 18.10.2026 № ffc1f29499 · стр. 130 из 155

Развёртка стены Г


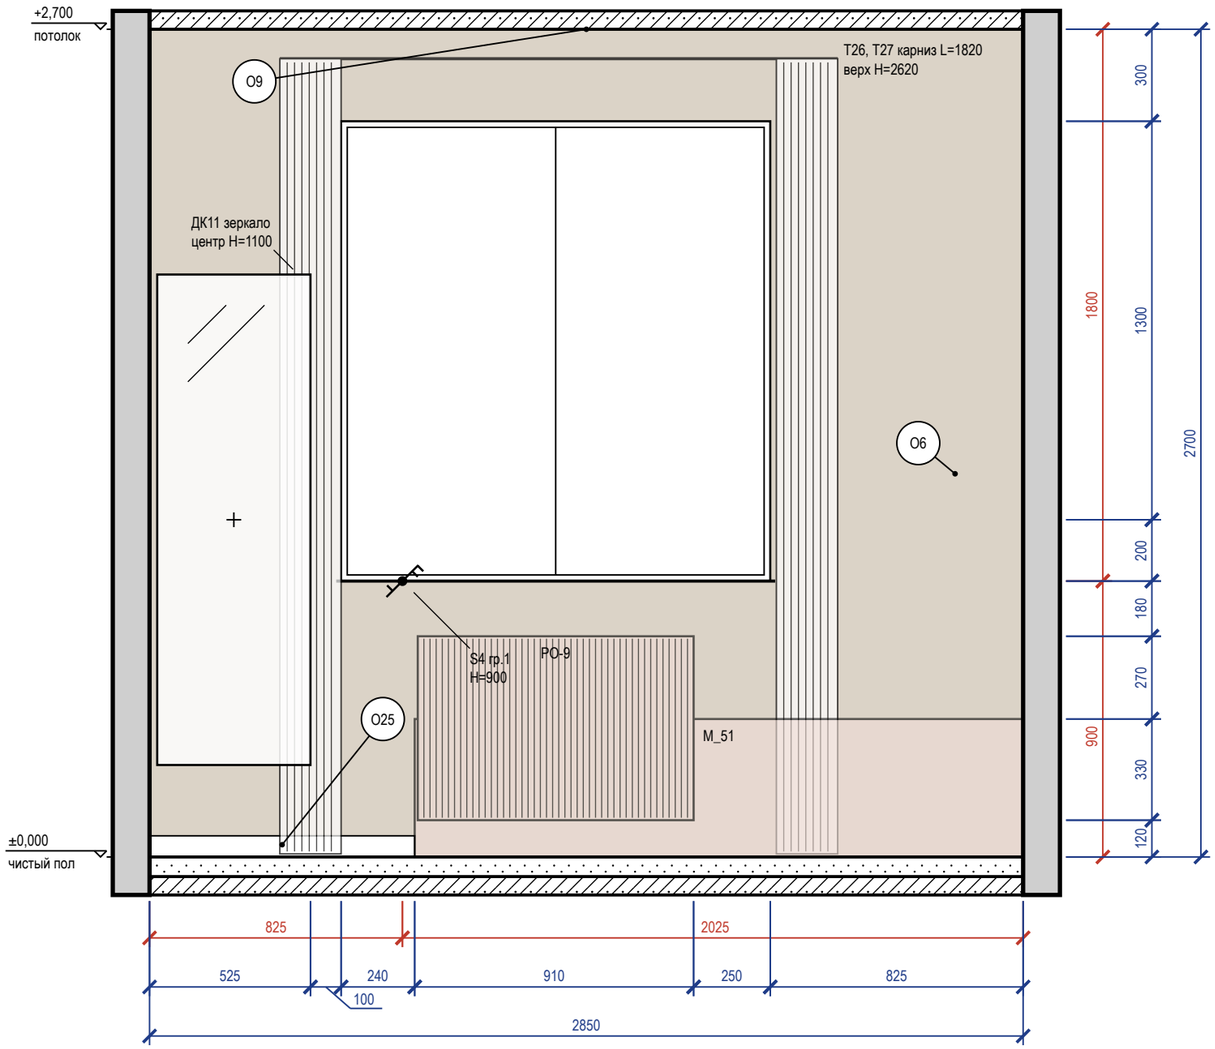


Схема развёрток (М 1:100)

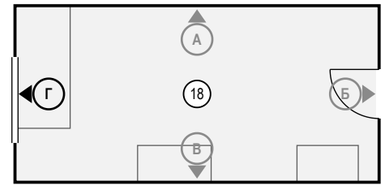

Ведомость отделки (на листе)

Марка	Поверхность	Материал, изделие	Цвет, код	Кол.
О6	стены	окраска, Farrow & Ball Modern Emulsion, матовая, подготовка Q3	Farrow & Ball No. 226 «Joa's White»	5,6 м²
О9	потолок	окраска, Tikkurila Anti-Reflex 2, глубокоматовая, подготовка Q3	Little Greene No. 105 «Slaked Lime»	17,1 м²
О25	плинтус	плинтус МДФ, Orac Decor Contour (Luxxus), h 69 мм, SX165	Farrow & Ball No. 226 «Joa's White»	0,9 м

Визуализация этой стены



Примечания

1. Размеры — в мм от чистовых поверхностей стен; условные обозначения и общие указания — лист 2.
2. Картины и зеркала крепить к основанию по паспорту изделия (закладные и анкеры — в перечне скрытых работ); крест — ось центра предмета.
3. Карнизы (шины) — по ведомости текстиля декоратора; длина L и верх H — по развёртке, крепление — до окраски потолка.

					Проект: Дом 331 м²
	Лист	№ док.	Подпись	Дата	Развёртка стены Г. Спальня 3 (пом. 18)
Дизайнер	Кырлан А.С.			19.10.26	

Стадия	Лист	Листов
П	131	155

выпуск 18.10.2026 № ffc1f29499 · стр. 131 из 155



					Проект: Дом 331 м²
	Лист	№ док.	Подпись	Дата	
Дизайнер	Кырлан А.С.			19.10.26	Визуализация: Спальня 4

Стадия	Лист	Листов
П	132	155

выпуск 18.10.2026 № ffc1f29499 · стр. 132 из 155



					Проект: Дом 331 м²
	Лист	№ док.	Подпись	Дата	
Дизайнер	Кырлан А.С.			19.10.26	Визуализация: Спальня 4

Стадия	Лист	Листов
П	133	155

выпуск 18.10.2026 № ffc1f29499 · стр. 133 из 155

Развёртка стены А


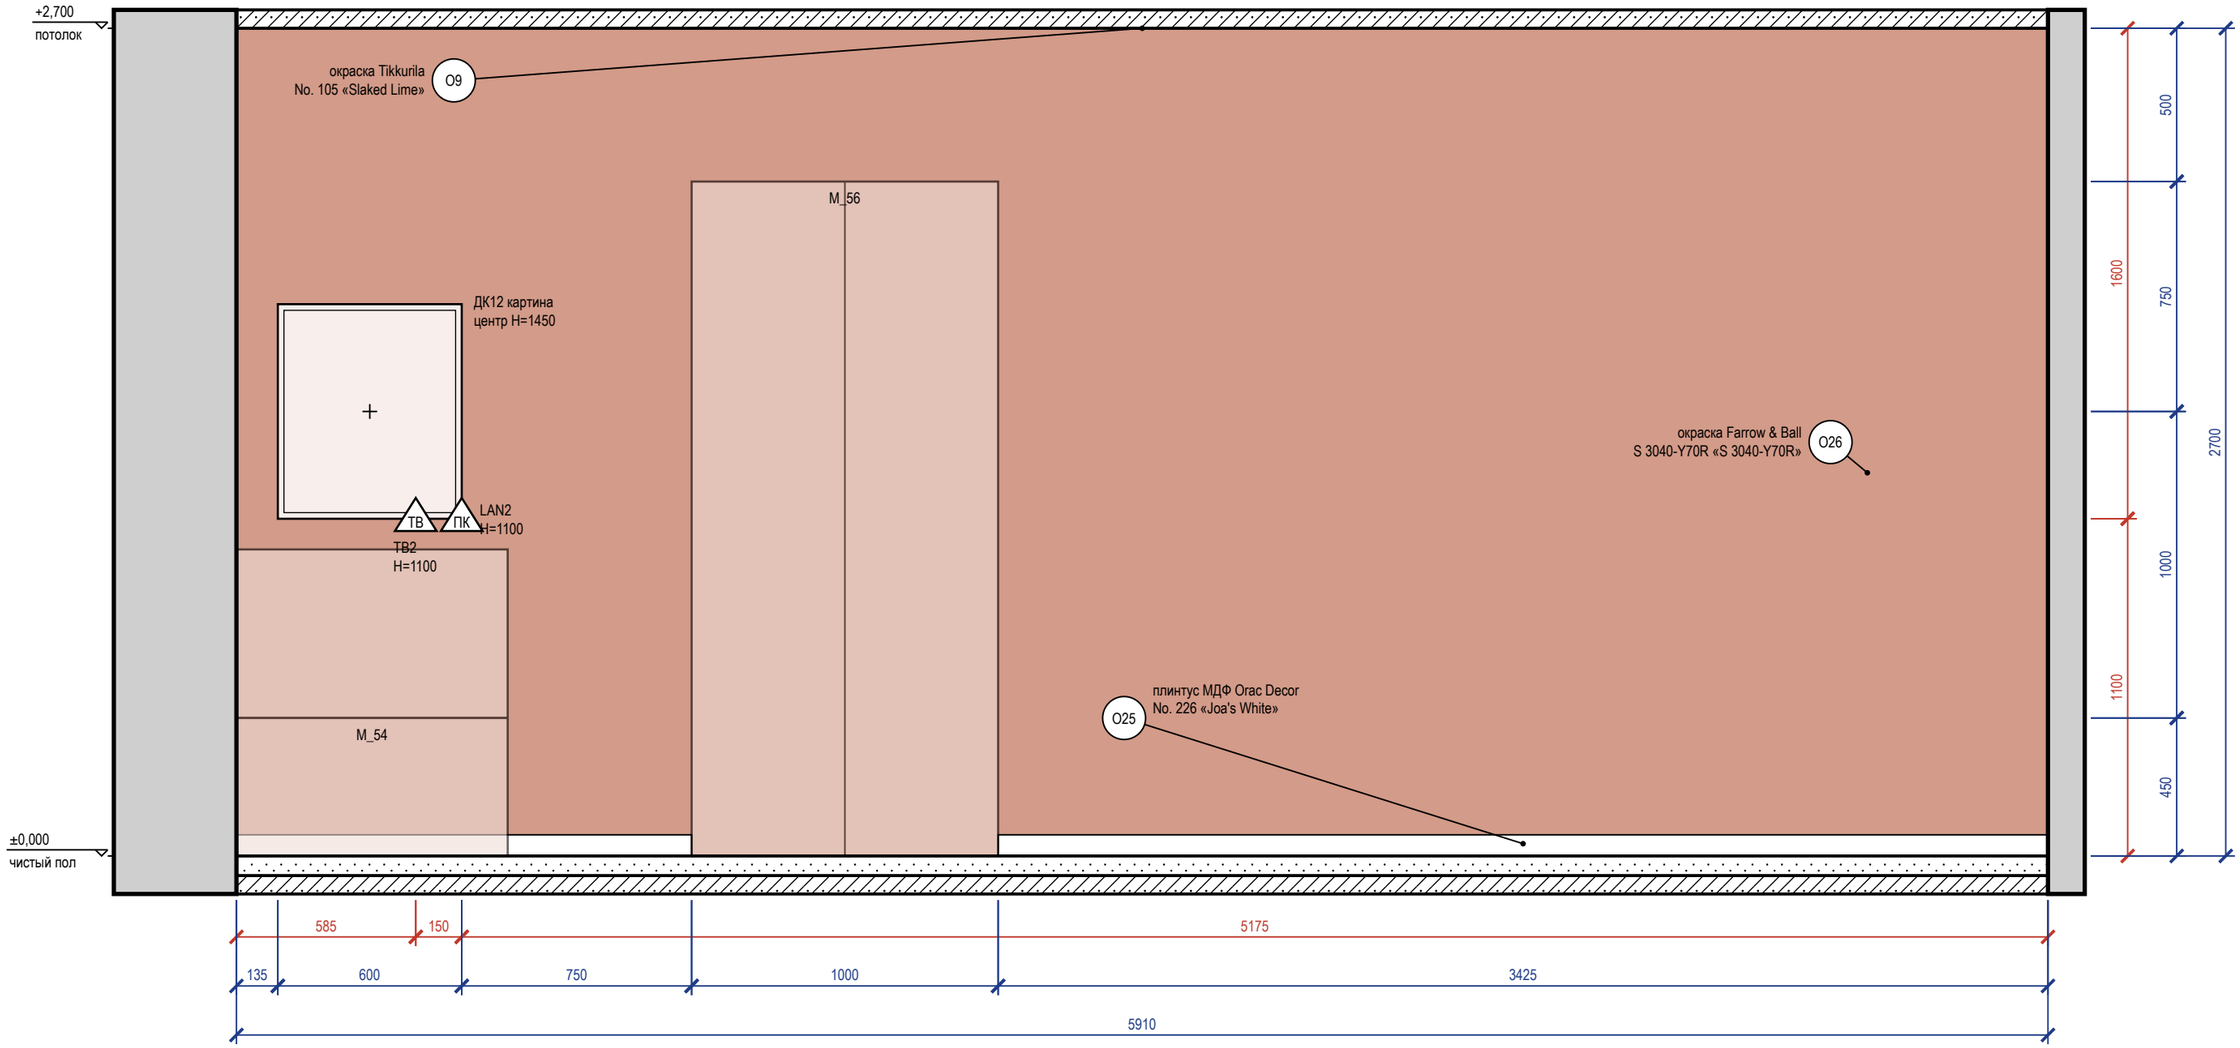



Схема развёрток (М 1:100)

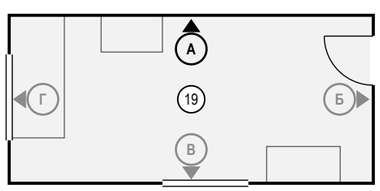

Ведомость отделки (на листе)

Марка	Поверхность	Материал, изделие	Цвет, код	Кол.
O9	потолок	окраска, Tikkurila Anti-Reflex 2, глубокоматовая, подготовка Q3	Little Greene No. 105 «Slaked Lime»	16,3 м²
O25	плинтус	плинтус МДФ, Orac Decor Contour (Luxxus), h 69 мм, SX165	Farrow & Ball No. 226 «Joa's White»	4,9 м
O26	акцентная стена	окраска, Farrow & Ball Modern Emulsion, матовая, подготовка Q3	NCS S 3040-Y70R «S 3040-Y70R»	16 м²

Визуализация этой стены — лист 132

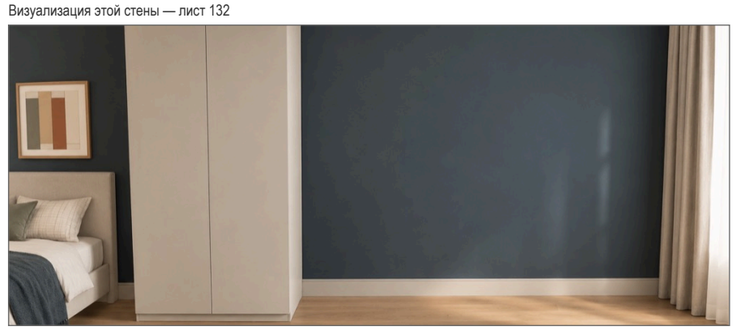

Примечания

1. Размеры — в мм от чистовых поверхностей стен; условные обозначения и общие указания — лист 2.
2. Картины и зеркала крепить к основанию по паспорту изделия (закладные и анкеры — в перечне скрытых работ); крест — ось центра предмета.

					Проект: Дом 331 м²
	Лист	№ док.	Подпись	Дата	Развёртка стены А. Спальня 4 (пом. 19)
Дизайнер	Кырлан А.С.			19.10.26	

Стадия	Лист	Листов
П	134	155

выпуск 18.10.2026 № ffc1f29499 · стр. 134 из 155

Развёртка стены Б


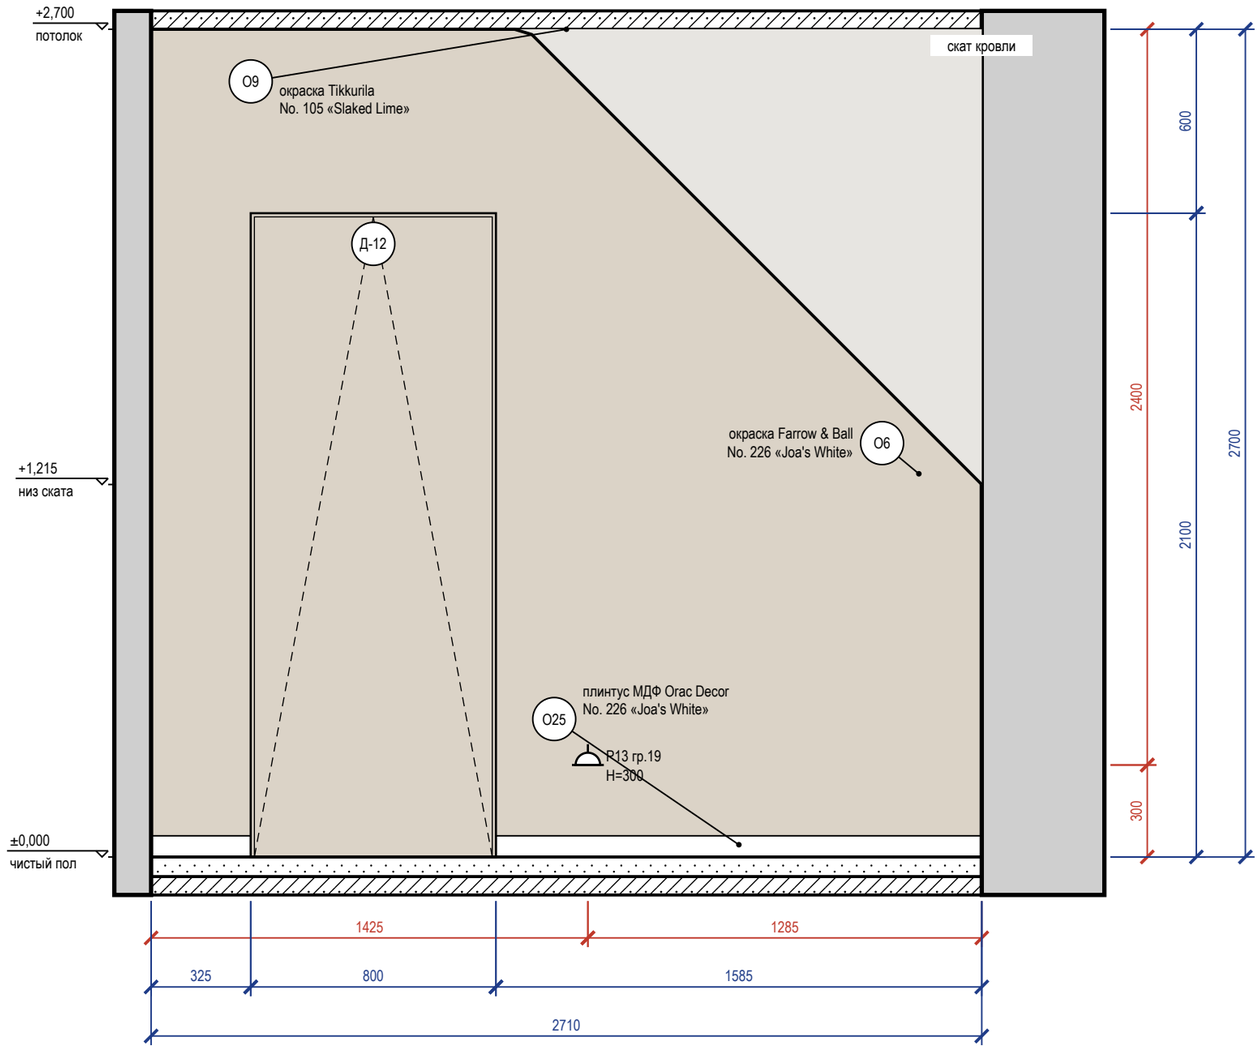


Схема развёрток (М 1:100)

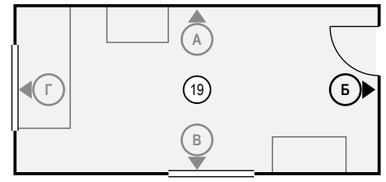

Ведомость отделки (на листе)

Марка	Поверхность	Материал, изделие	Цвет, код	Кол.
О6	стены	окраска, Farrow & Ball Modern Emulsion, матовая, подготовка Q3	Farrow & Ball No. 226 «Joa's White»	5,6 м²
О9	потолок	окраска, Tikkurila Anti-Reflex 2, глубокоматовая, подготовка Q3	Little Greene No. 105 «Slaked Lime»	16,3 м²
О25	плинтус	плинтус МДФ, Orac Decor Contour (Luxxus), h 69 мм, SX165	Farrow & Ball No. 226 «Joa's White»	1,9 м

Примечания

1. Размеры — в мм от чистовых поверхностей стен; условные обозначения и общие указания — лист 2.
2. Двери скрытого монтажа — полотно в плоскости стены, отделка стены по полотну, плинтус прерывается у короба (узел — на листе узлов).

					Проект: Дом 331 м²
	Лист	№ док.	Подпись	Дата	Развёртка стены Б. Спальня 4 (пом. 19)
Дизайнер	Кырлан А.С.			19.10.26	

Стадия	Лист	Листов
П	135	155

выпуск 18.10.2026 № ffc1f29499 · стр. 135 из 155

Развёртка стены В


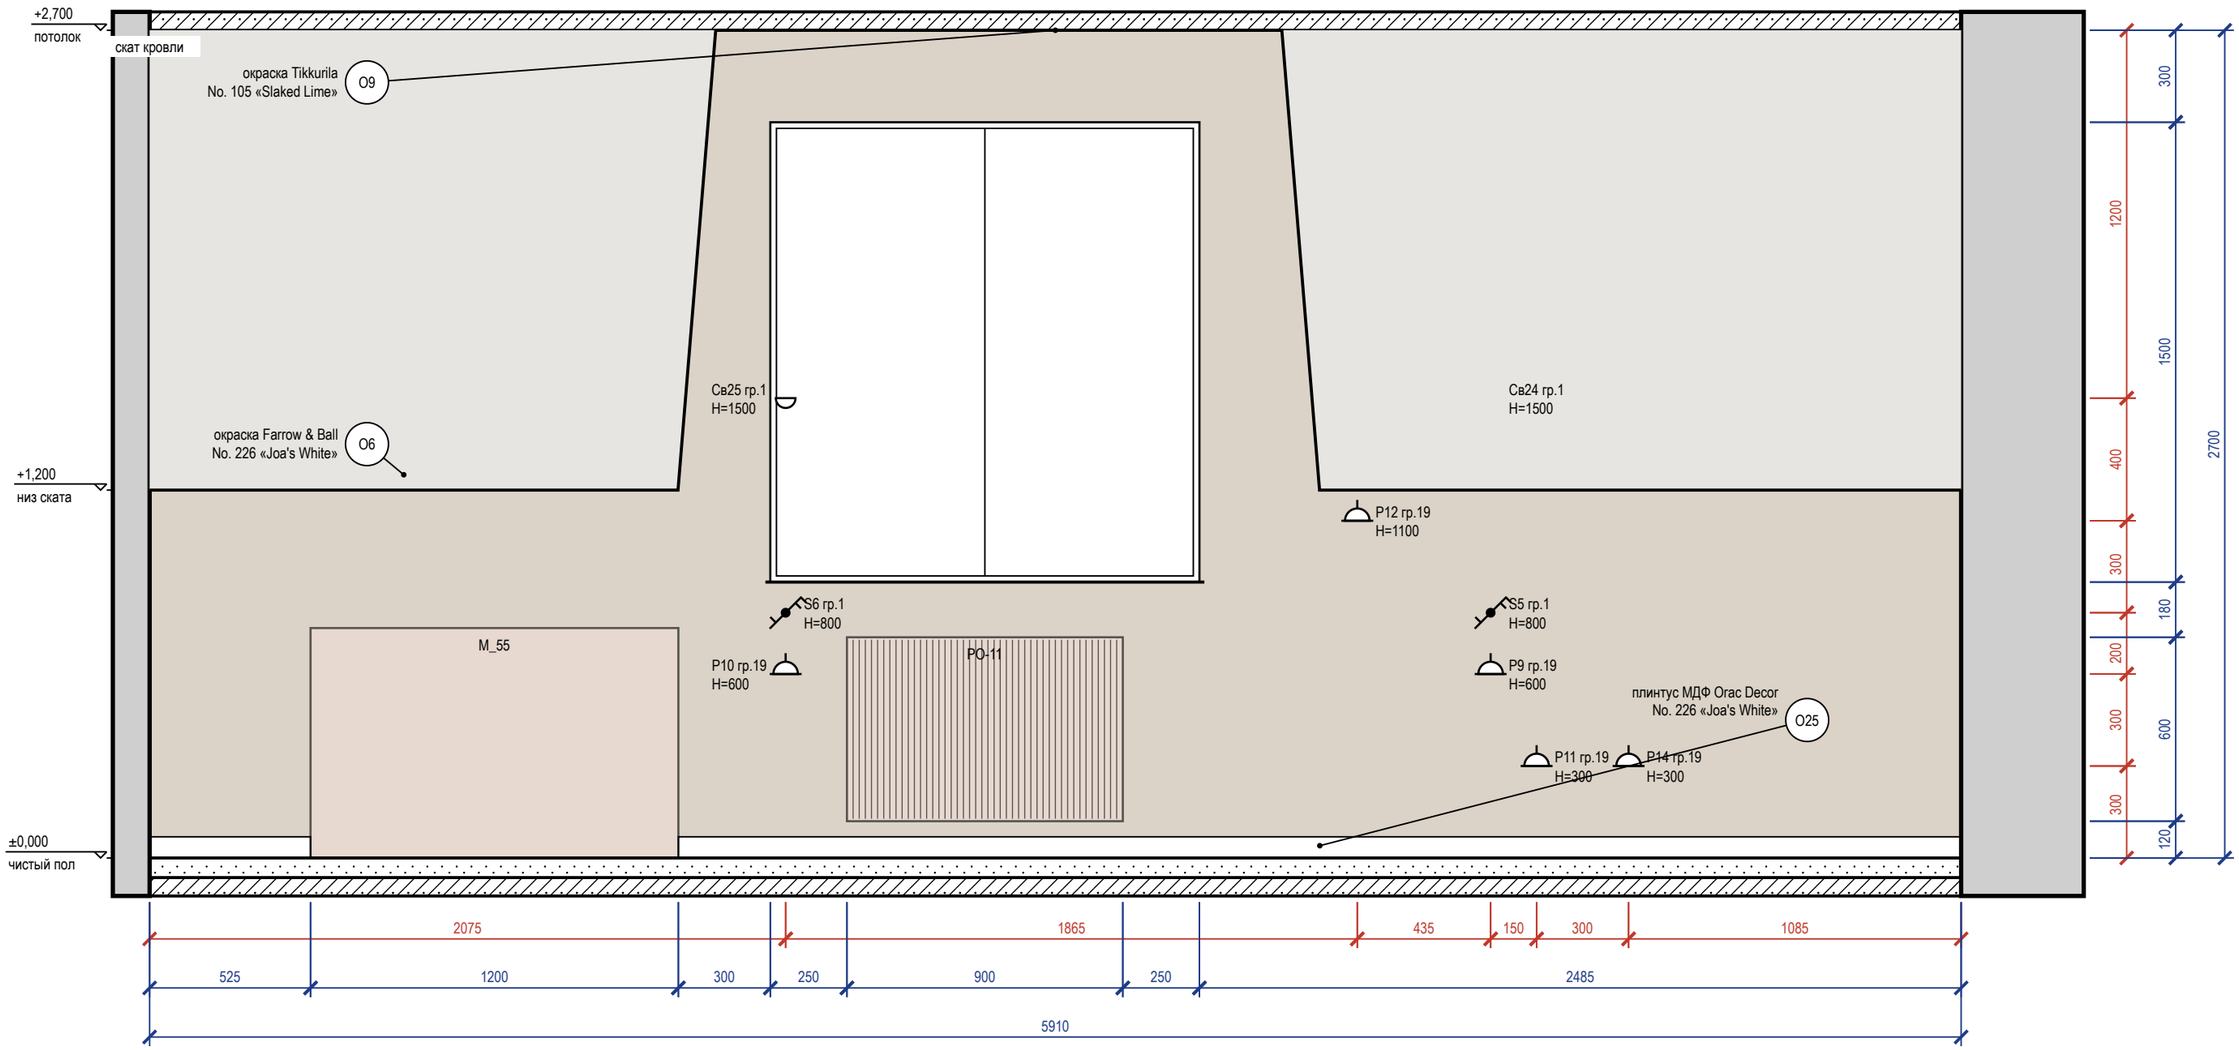



Схема развёрток (М 1:100)

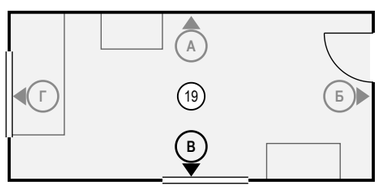

Ведомость отделки (на листе)

Марка	Поверхность	Материал, изделие	Цвет, код	Кол.
О6	стены	окраска, Farrow & Ball Modern Emulsion, матовая, подготовка Q3	Farrow & Ball No. 226 «Joa's White»	13,9 м²
О9	потолок	окраска, Tikkurila Anti-Reflex 2, глубокоматовая, подготовка Q3	Little Greene No. 105 «Slaked Lime»	16,3 м²
О25	плинтус	плинтус МДФ, Orac Decor Contour (Luxxus), h 69 мм, SX165	Farrow & Ball No. 226 «Joa's White»	4,7 м

Визуализация этой стены — лист 133

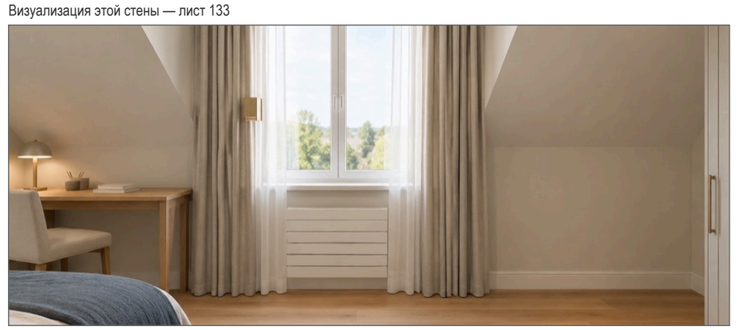

Примечания

1. Размеры — в мм от чистовых поверхностей стен; условные обозначения и общие указания — лист 2.

	Лист	№ док.	Подпись	Дата	Проект: Дом 331 м²
Дизайнер	Кырлан А.С.			19.10.26	Развёртка стены В. Спальня 4 (пом. 19)

Стадия	Лист	Листов
П	136	155

выпуск 18.10.2026 № ffc1f29499 · стр. 136 из 155

Развёртка стены Г


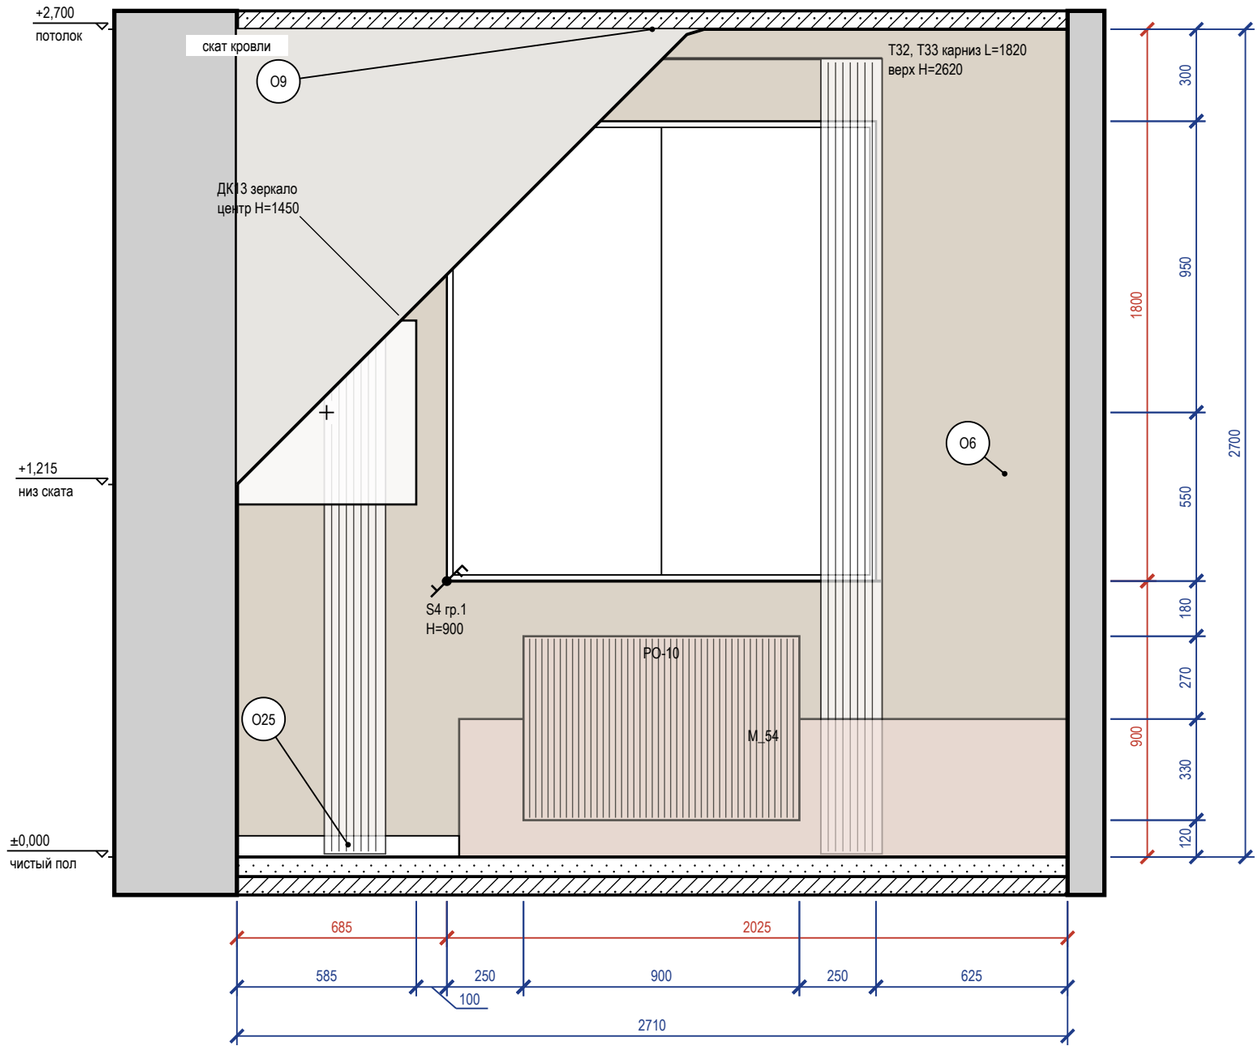


Схема развёрток (М 1:100)

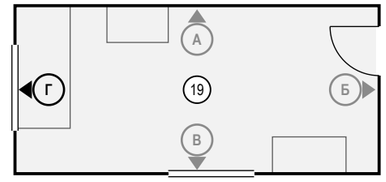

Ведомость отделки (на листе)

Марка	Поверхность	Материал, изделие	Цвет, код	Кол.
О6	стены	окраска, Farrow & Ball Modern Emulsion, матовая, подготовка Q3	Farrow & Ball No. 226 «Joa's White»	5,2 м²
О9	потолок	окраска, Tikkurila Anti-Reflex 2, глубокоматовая, подготовка Q3	Little Greene No. 105 «Slaked Lime»	16,3 м²
О25	плинтус	плинтус МДФ, Orac Decor Contour (Luxxus), h 69 мм, SX165	Farrow & Ball No. 226 «Joa's White»	0,7 м

Примечания

1. Размеры — в мм от чистовых поверхностей стен; условные обозначения и общие указания — лист 2.
2. Картины и зеркала крепить к основанию по паспорту изделия (закладные и анкеры — в перечне скрытых работ); крест — ось центра предмета.
3. Карнизы (шины) — по ведомости текстиля декоратора; длина L и верх H — по развёртке, крепление — до окраски потолка.
4. Линии узора (швы плитки, складки штор, рёбра радиаторов) прерываются у знаков и выносок — просвет между линиями не менее 0,7 мм.

					Проект: Дом 331 м²
	Лист	№ док.	Подпись	Дата	
Дизайнер	Кырлан А.С.			19.10.26	Развёртка стены Г. Спальня 4 (пом. 19)

Стадия	Лист	Листов
П	137	155

выпуск 18.10.2026 № ffc1f29499 · стр. 137 из 155



					Проект: Дом 331 м²
	Лист	№ док.	Подпись	Дата	
Дизайнер	Кырлан А.С.			19.10.26	Визуализация: Санузел 2

Стадия	Лист	Листов
П	138	155

выпуск 18.10.2026 ffc1f29499 · стр. 138 из 155

Развёртка стены А


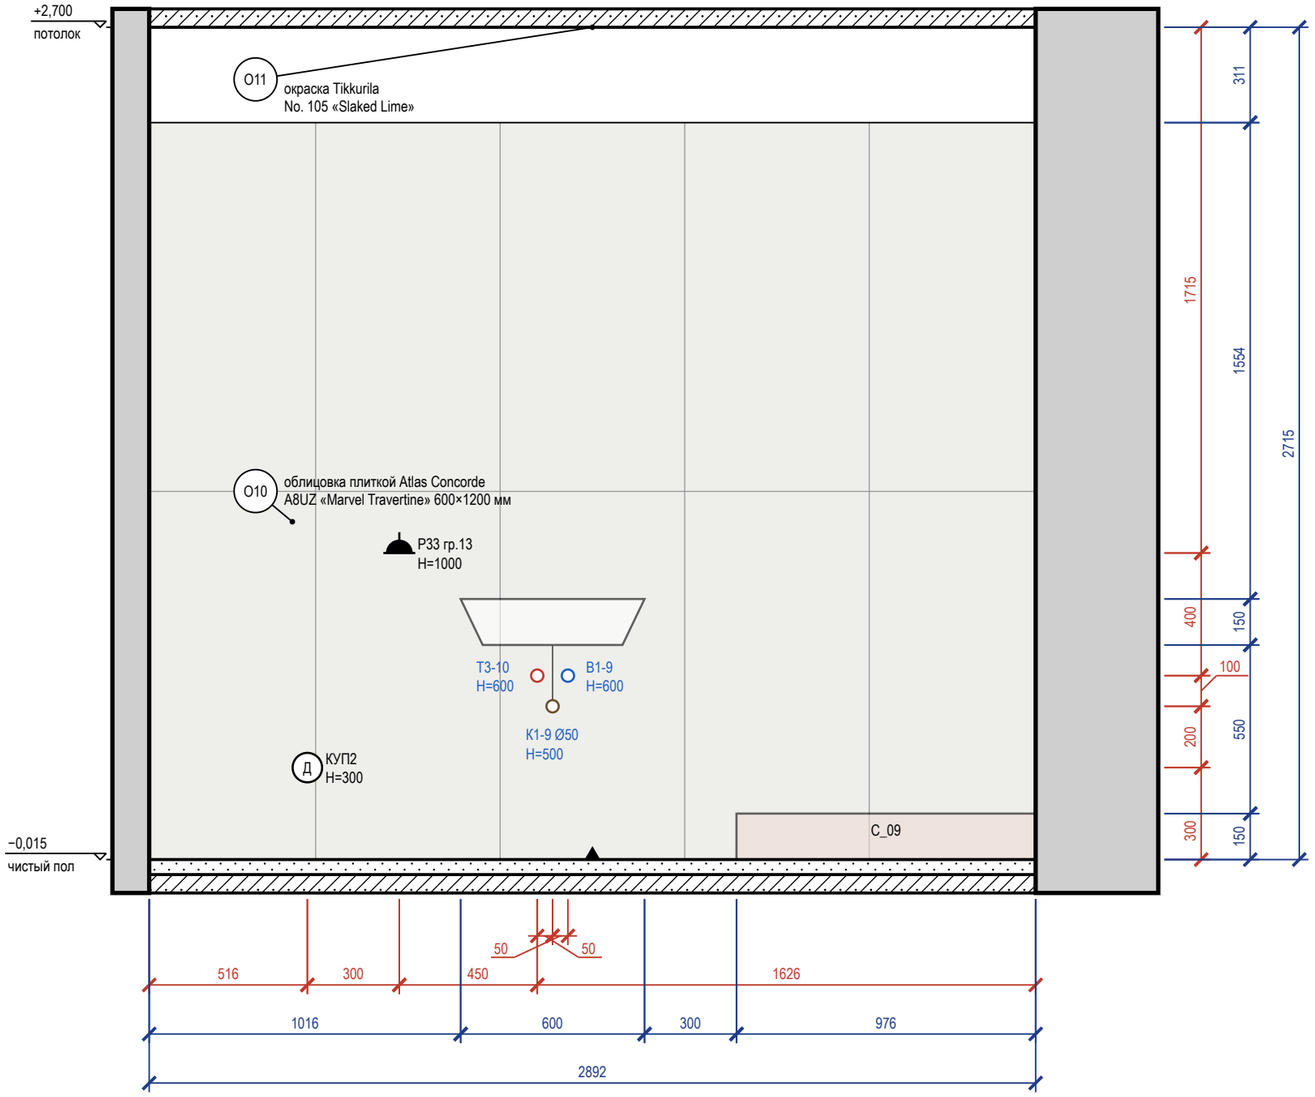


Схема развёрток (М 1:100)

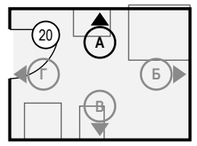

Ведомость отделки (на листе)

Марка	Поверхность	Материал, изделие	Цвет, код	Кол.
О10	стены	облицовка плиткой, Atlas Concorde Marvel Travertine, 600×1200×9 мм, A8UZ, затирка CG2WA	Atlas Concorde A8UZ «Marvel Travertine»	7 м²
О11	потолок	окраска, Tikkurila Luja 7, матовая, подготовка Q3	Little Greene No. 105 «Slaked Lime»	6,3 м²

Примечания

1. Размеры — в мм от чистовых поверхностей стен; условные обозначения и общие указания — лист 2.
2. Схема мебели, приборов и декора не является технической документацией для производства мебели; габариты — по паспортам изделий.
3. Выводы ВК — коды и высоты по листу выводов сантехники.
4. Облицовка — по сетке швов 2 мм, раскладка от оси стены (треугольник у пола), целые ряды от пола; подрезки — по листу раскладки плитки.
5. Гидроизоляция в 2 слоя, заход на стены 200 мм — до облицовки, с актом скрытых работ и тестом проливом (узел — на листе узлов).

	Лист	№ док.	Подпись	Дата	Проект: Дом 331 м²			
Дизайнер	Кырлан А.С.			19.10.26	Развёртка стены А. Санузел 2 (пом. 20)	Стадия	Лист	Листов
						П	139	155

выпуск 18.10.2026 № ffc1f29499 · стр. 139 из 155

Развёртка стены Б


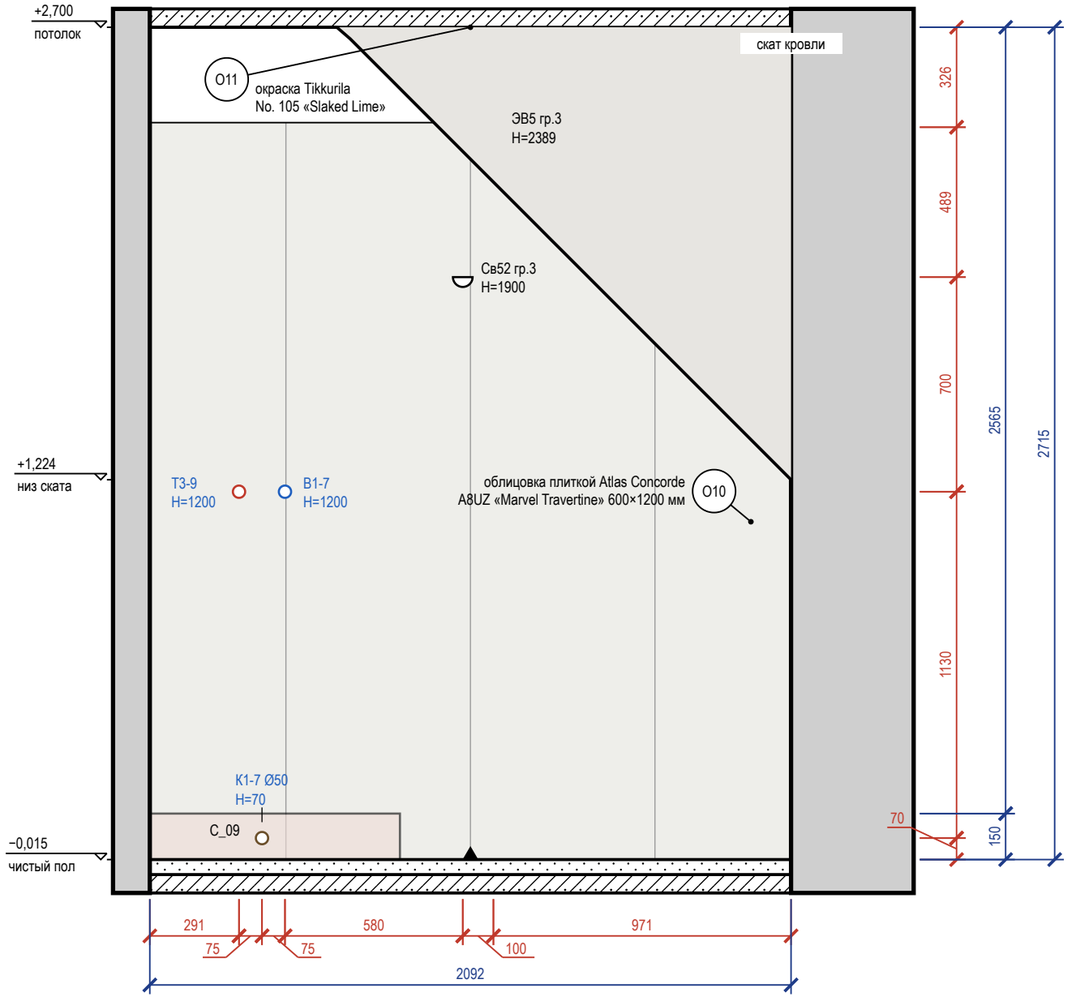


Схема развёрток (М 1:100)

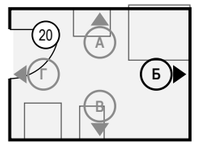

Ведомость отделки (на листе)

Марка	Поверхность	Материал, изделие	Цвет, код	Кол.
О10	стены	облицовка плиткой, Atlas Concorde Marvel Travertine, 600×1200×9 мм, A8UZ, затирка CG2WA	Atlas Concorde A8UZ «Marvel Travertine»	5 м²
О11	потолок	окраска, Tikkurila Luja 7, матовая, подготовка Q3	Little Greene No. 105 «Slaked Lime»	6,3 м²

Визуализация этой стены — лист 138



Примечания

1. Размеры — в мм от чистовых поверхностей стен; условные обозначения и общие указания — лист 2.
2. Схема мебели, приборов и декора не является технической документацией для производства мебели; габариты — по паспортам изделий.
3. Выводы ВК — коды и высоты по листу выводов сантехники.
4. Облицовка — по сетке швов 2 мм, раскладка от оси стены (треугольник у пола), целые ряды от пола; подрезки — по листу раскладки плитки.
5. Гидроизоляция в 2 слоя, заход на стены 200 мм — до облицовки, с актом скрытых работ и тестом проливом (узел — на листе узлов).

					Проект: Дом 331 м²
	Лист	№ док.	Подпись	Дата	Развёртка стены Б. Санузел 2 (пом. 20)
Дизайнер	Кырлан А.С.			19.10.26	

Стадия	Лист	Листов
П	140	155

Развёртка стены В


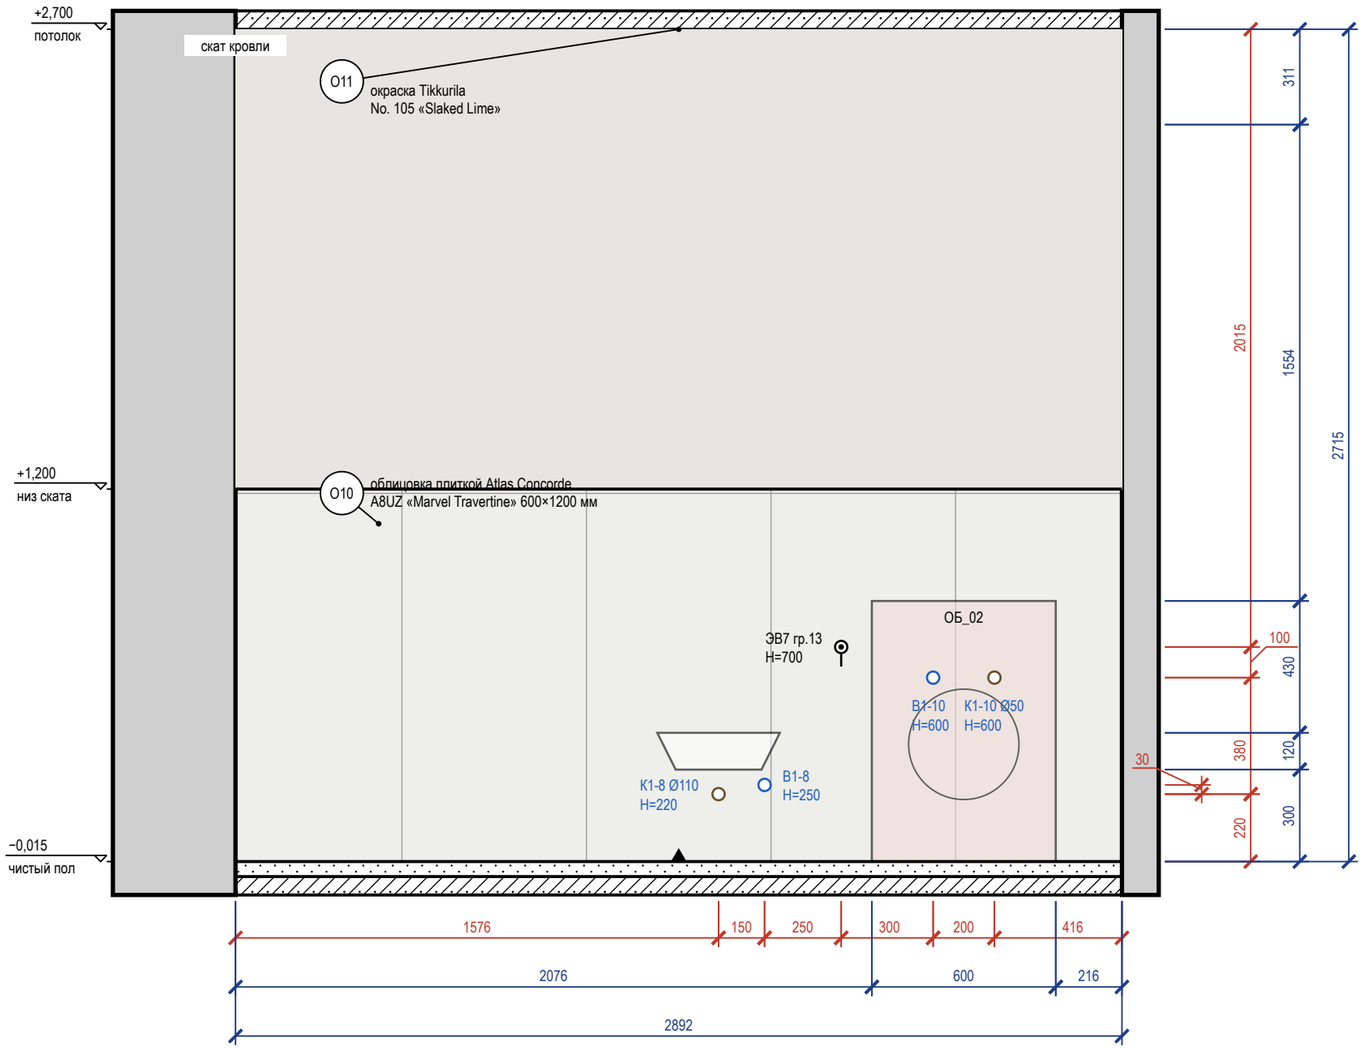


Схема развёрток (М 1:100)

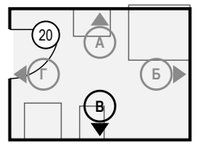

Ведомость отделки (на листе)

Марка	Поверхность	Материал, изделие	Цвет, код	Кол.
О10	стены	облицовка плиткой, Atlas Concorde Marvel Travertine, 600×1200×9 мм, A8UZ, затирка CG2WA	Atlas Concorde A8UZ «Marvel Travertine»	7 м²
О11	потолок	окраска, Tikkurila Luja 7, матовая, подготовка Q3	Little Greene No. 105 «Slaked Lime»	6,3 м²

Примечания

1. Размеры — в мм от чистовых поверхностей стен; условные обозначения и общие указания — лист 2.
2. Схема мебели, приборов и декора не является технической документацией для производства мебели; габариты — по паспортам изделий.
3. Выводы ВК — коды и высоты по листу выводов сантехники.
4. Облицовка — по сетке швов 2 мм, раскладка от оси стены (треугольник у пола), целые ряды от пола; подрезки — по листу раскладки плитки.
5. Гидроизоляция в 2 слоя, заход на стены 200 мм — до облицовки, с актом скрытых работ и тестом проливом (узел — на листе узлов).

					Проект: Дом 331 м²
	Лист	№ док.	Подпись	Дата	Развёртка стены В. Санузел 2 (пом. 20)
Дизайнер	Кырлан А.С.			19.10.26	

Стадия	Лист	Листов
П	141	155

выпуск 18.10.2026 № ffc1f29499 · стр. 141 из 155

Развёртка стены Г


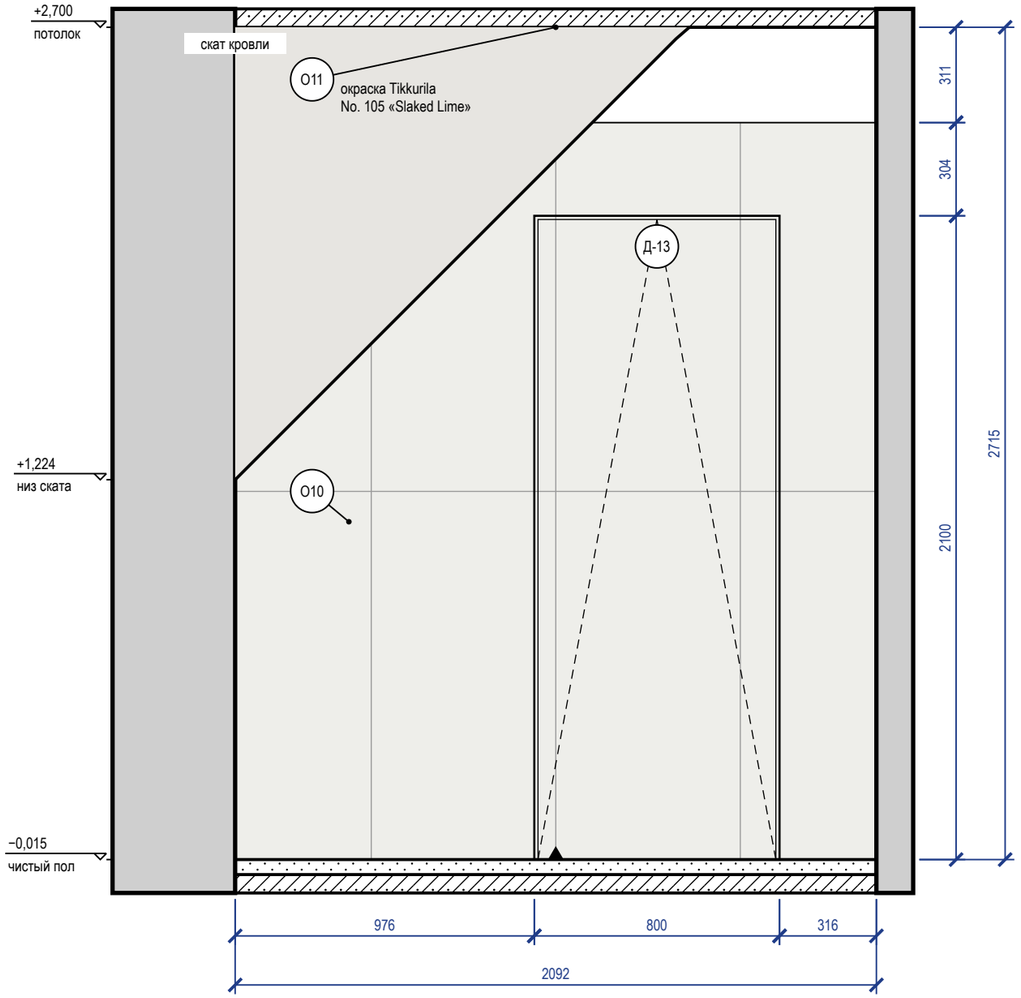


Схема развёрток (М 1:100)

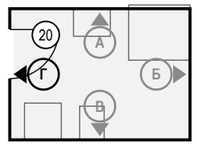

Ведомость отделки (на листе)

Марка	Поверхность	Материал, изделие	Цвет, код	Кол.
О10	стены	облицовка плиткой, Atlas Concorde Marvel Travertine, 600×1200×9 мм, A8UZ, затирка CG2WA	Atlas Concorde A8UZ «Marvel Travertine»	3,3 м²
О11	потолок	окраска, Tikkurila Luja 7, матовая, подготовка Q3	Little Greene No. 105 «Slaked Lime»	6,3 м²

Примечания


1. Размеры — в мм от чистовых поверхностей стен; условные обозначения и общие указания — лист 2.
2. Облицовка — по сетке швов 2 мм, раскладка от оси стены (треугольник у пола), целые ряды от пола; подрезки — по листу раскладки плитки.
3. Гидроизоляция в 2 слоя, заход на стены 200 мм — до облицовки, с актом скрытых работ и тестом проливом (узел — на листе узлов).
4. Двери скрытого монтажа — полотно в плоскости стены, отделка стены по полотну, плинтус прерывается у короба (узел — на листе узлов).

					Проект: Дом 331 м²
	Лист	№ док.	Подпись	Дата	Развёртка стены Г. Санузел 2 (пом. 20)
Дизайнер	Кырлан А.С.			19.10.26	


Стадия	Лист	Листов
П	142	155

выпуск 18.10.2026 № ffc1f29499 · стр. 142 из 155


Общий вид

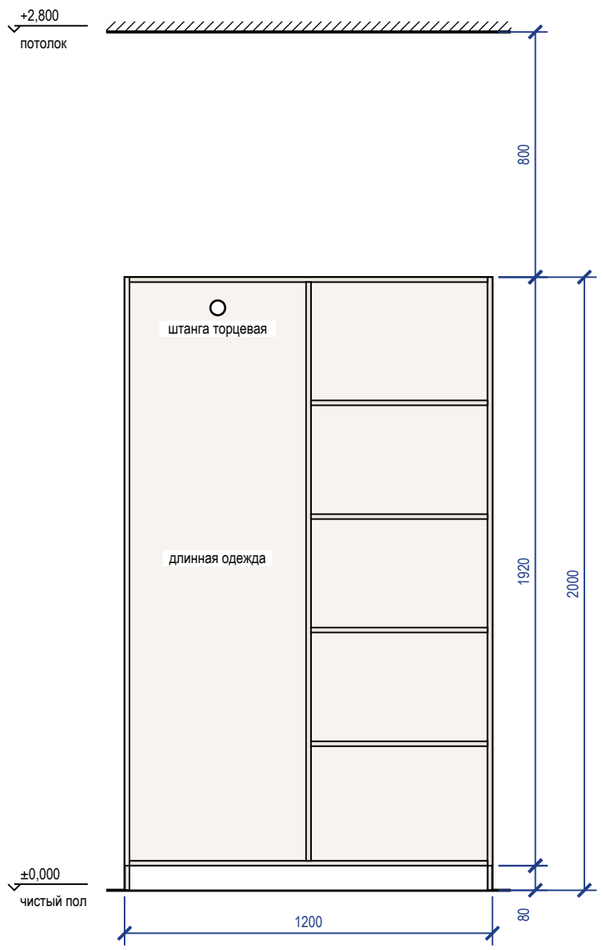


Наполнение, размеры в свету

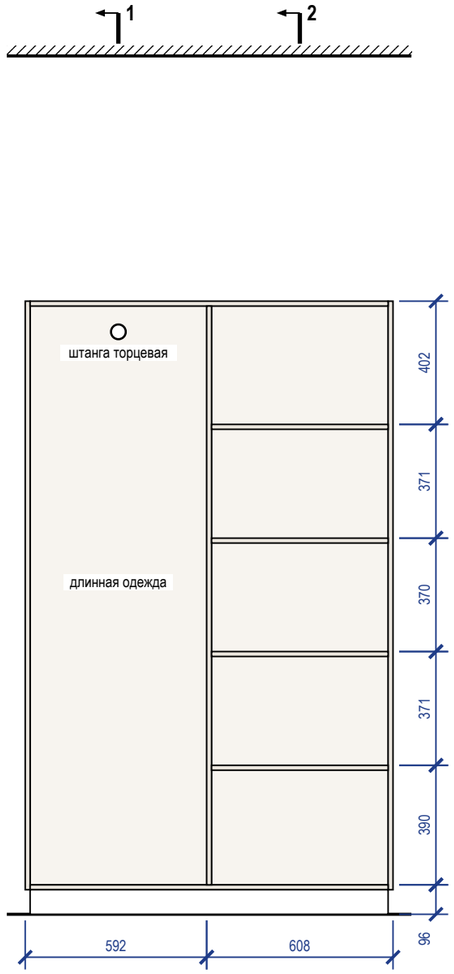

Разрез 1-1

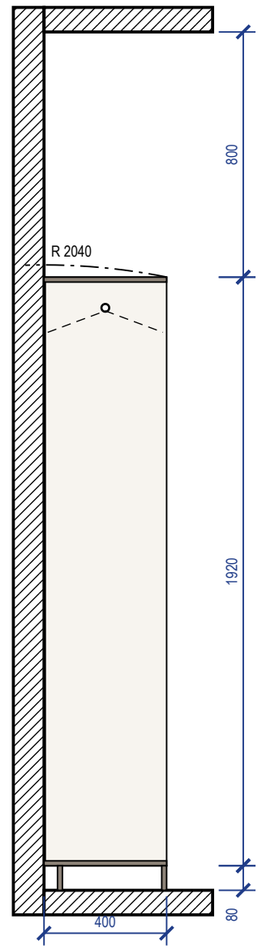


Разрез 2-2

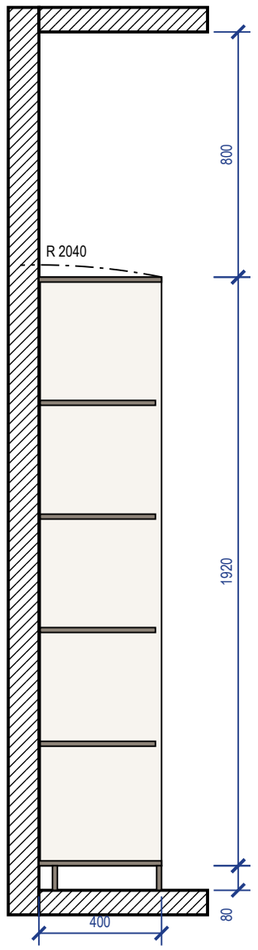

Примечания

1. Размеры — в мм по чистовой отделке; изделие 1200×400×2000 (Ш×Г×В). Перед раскроем — контрольный замер цеха после чистовой отделки стен, пола и потолка.
2. Корпус — ЛДСП 16 мм, задняя стенка ХДФ 4 мм в паз, цоколь 80 мм на регулируемых опорах; открытая система без фасадов, ящики с фасадами.
3. Кромка: скрытые торцы 0,4 мм, видимые 2 мм (ПВХ/АБС).
4. Номинальные зазоры: между фасадами ящиков 3 мм, фасад ящика — стойка 2 мм.
5. Ящики — направляющие полного выдвижения NL 350 (внутренняя глубина 396 мм ≥ NL + 3); присадка по 32-й системе — выполняет цех.
6. Зазор до потолка 800 мм.
7. Подъём корпуса: диагональ боковины $\sqrt{(2000^2 + 400^2)} = 2040$ мм < 2800 мм до потолка — корпус собирается лёжа и поднимается поворотом.
8. Крепление к стене от опрокидывания — уголки 2 шт. к несущему основанию (монтажная схема шкафов).

3D орто

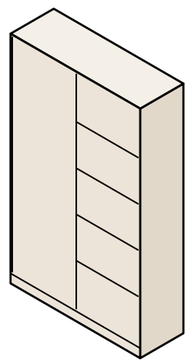


					Проект: Дом 331 м²
	Лист	№ док.	Подпись	Дата	Система хранения M_17
Дизайнер	Кырлан А.С.			19.10.26	


Стадия	Лист	Листов
П	Д_1	155

выпуск 18.10.2026 № ffc1f29499 · стр. 143 из 155


Общий вид

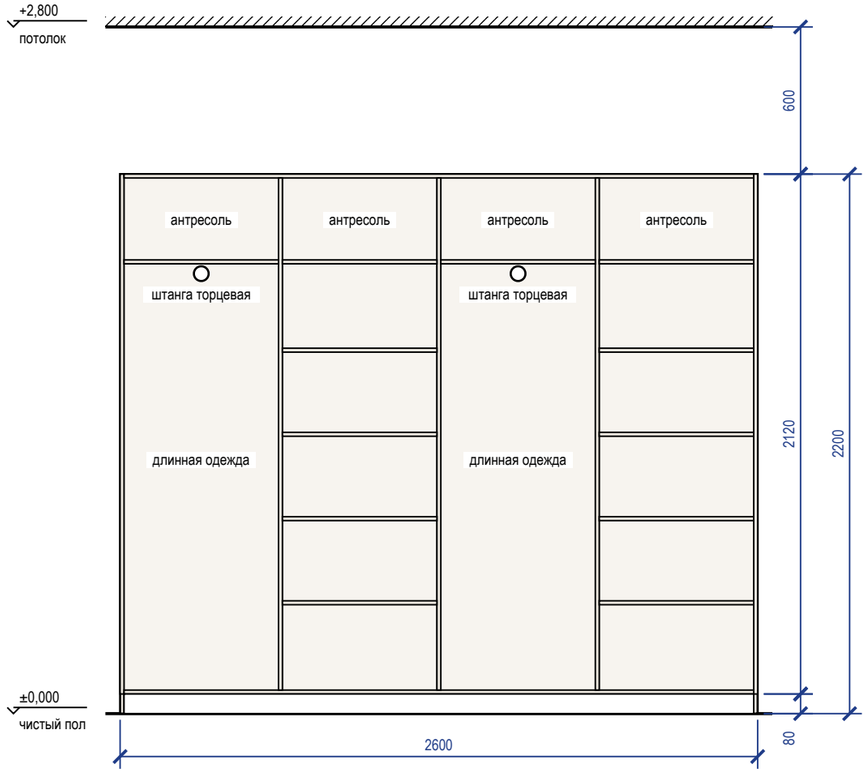


Наполнение, размеры в свету

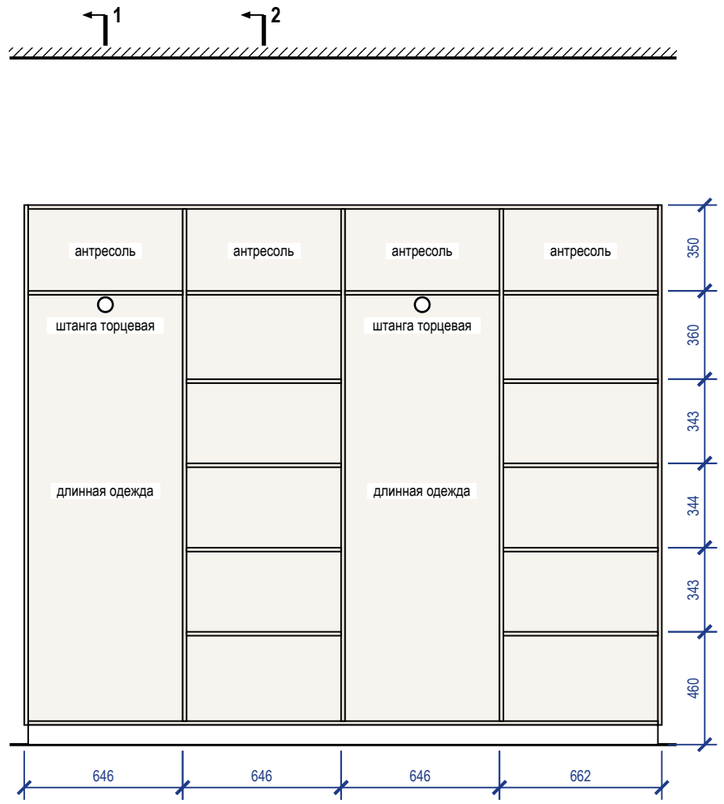

Разрез 1-1

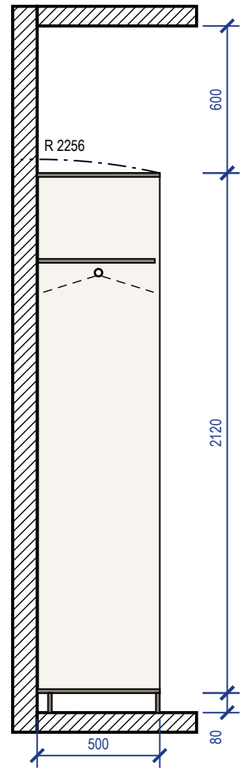


Разрез 2-2

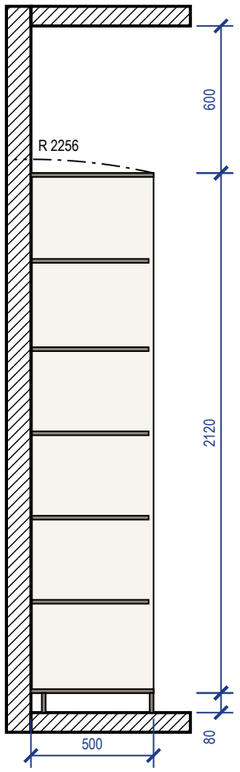

Примечания

1. Размеры — в мм по чистовой отделке; изделие 2600×500×2200 (Ш×Г×В). Перед раскроем — контрольный замер цеха после чистовой отделки стен, пола и потолка.
2. Корпус — ЛДСП 16 мм, задняя стенка ХДФ 4 мм в паз, цоколь 80 мм на регулируемых опорах; открытая система без фасадов, ящики с фасадами.
3. Кромка: скрытые торцы 0,4 мм, видимые 2 мм (ПВХ/АБС).
4. Номинальные зазоры: между фасадами ящиков 3 мм, фасад ящика — стойка 2 мм.
5. Ящики — направляющие полного выдвижения NL 450 (внутренняя глубина 496 мм ≥ NL + 3); присадка по 32-й системе — выполняет цех.
6. Зазор до потолка 600 мм.
7. Подъём корпуса: диагональ боковины $\sqrt{(2200^2 + 500^2)} = 2256$ мм < 2800 мм до потолка — корпус собирается лёжа и поднимается поворотом.
8. Крепление к стене от опрокидывания — уголки 2 шт. к несущему основанию (монтажная схема шкафов).


3D орто

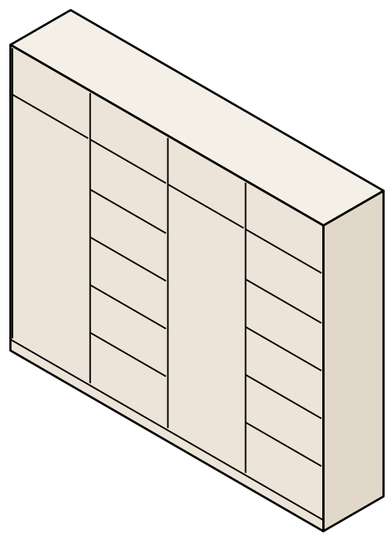


					Проект: Дом 331 м²
	Лист	№ док.	Подпись	Дата	
Дизайнер	Кырлан А.С.			19.10.26	Система хранения M_23
					Стадия: П; Лист: Д_2; Листов: 155

выпуск 18.10.2026 № ffc1f29499 · стр. 144 из 155


Вид с фасадами

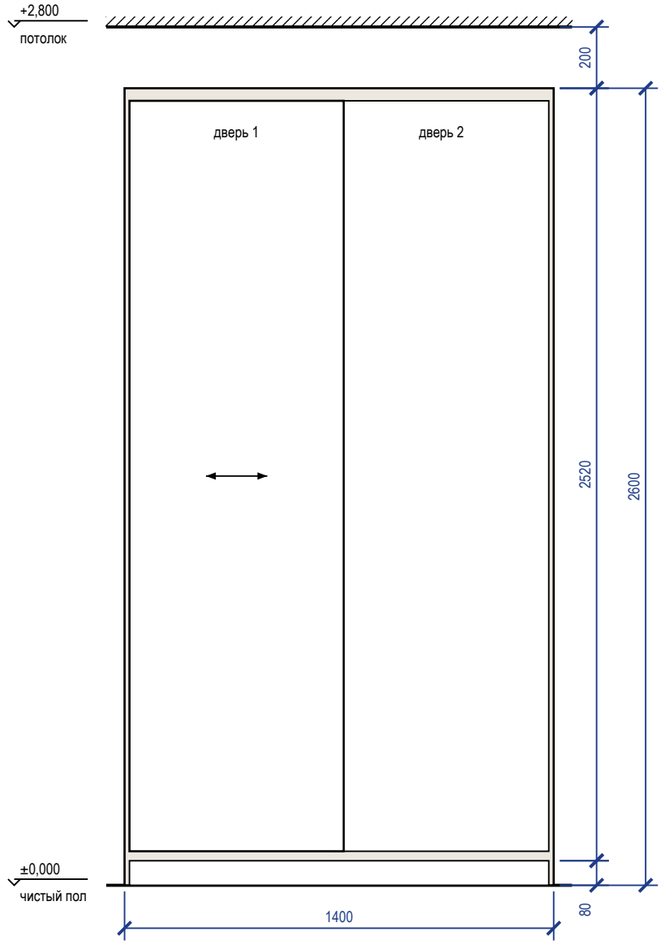


Вид без фасадов

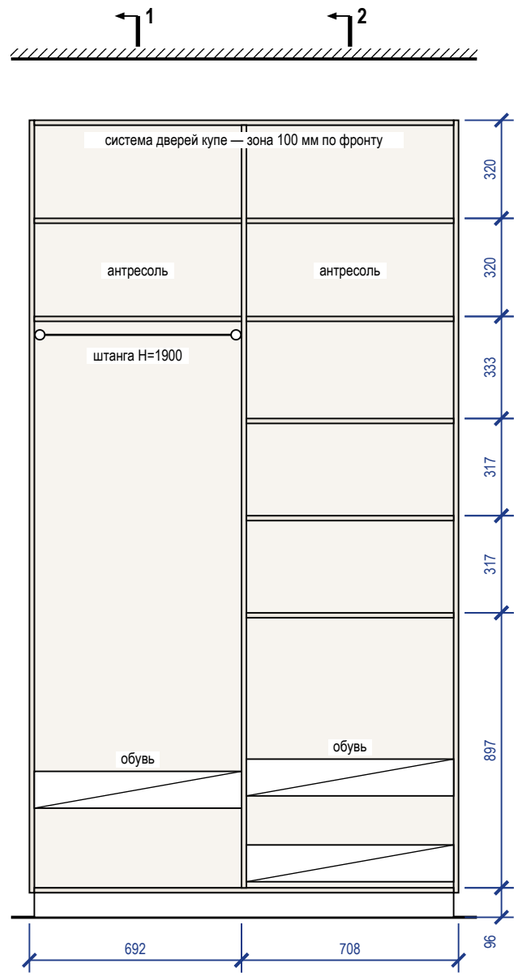

Разрез 1-1

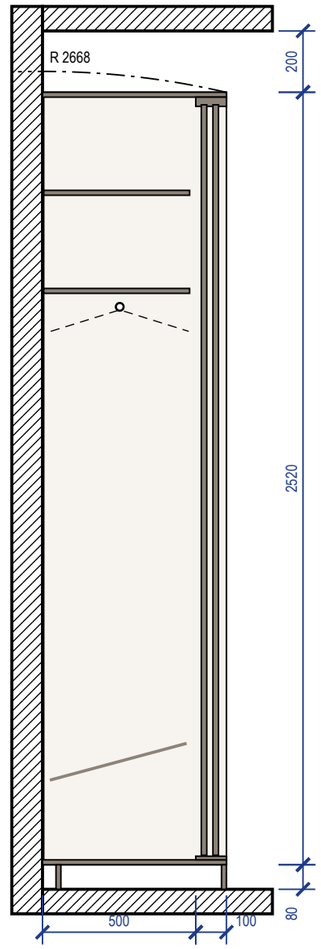


Разрез 2-2

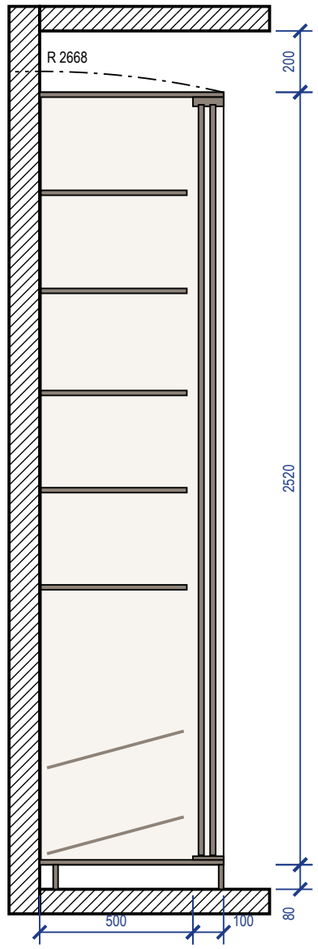

Примечания

1. Размеры — в мм по чистовой отделке; изделие 1400×600×2600 (Ш×Г×В). Перед раскроем — контрольный замер цеха после чистовой отделки стен, пола и потолка.
2. Корпус — ЛДСП 16 мм, задняя стенка ХДФ 4 мм в паз, цоколь 80 мм на регулируемых опорах; двери купе — ЛДСП 10 мм в алюминиевом профиле, нахлёст 30 мм, ширина двери 699 мм, высота — проём минус 40 мм; цвет — по колерной карте.
3. Кромка: скрытые торцы 0,4 мм, видимые 2 мм (ПВХ/АБС).
4. Номинальные зазоры: дверь купе — боковина 3 мм, фасад ящика — стойка 2 мм; ящики внутри купе — с накладкой 30 мм на стойке со стороны нахлёста дверей.
5. Ящики — направляющие полного выдвижения NL 450 (внутренняя глубина 496 мм ≥ NL + 3); присадка по 32-й системе — выполняет цех.
6. Зазор до потолка 200 мм.
7. Подъём корпуса: диагональ боковины $\sqrt{(2600^2 + 600^2)} = 2668$ мм < 2800 мм до потолка — корпус собирается лёжа и поднимается поворотом.
8. Крепление к стене от опрокидывания — уголки 2 шт. к несущему основанию (монтажная схема шкафов).

3D орто

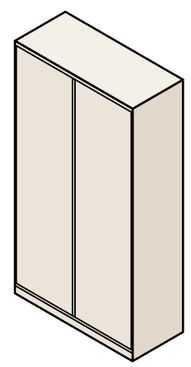


					Проект: Дом 331 м²
	Лист	№ док.	Подпись	Дата	
Дизайнер	Кырлан А.С.			19.10.26	Шкаф-купе М_24


Стадия	Лист	Листов
П	Д_3	155

выпуск 18.10.2026 № ffc1f29499 · стр. 145 из 155


Общий вид

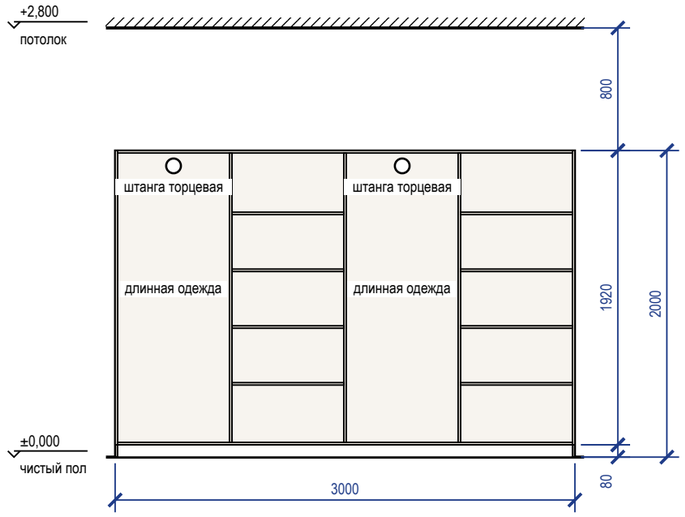


Наполнение, размеры в свету

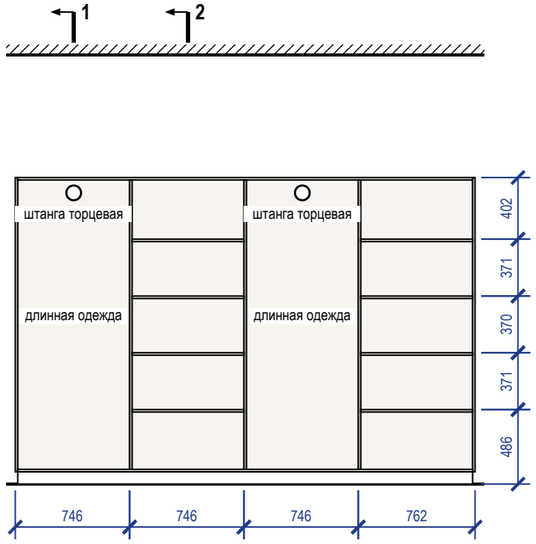

Разрез 1-1

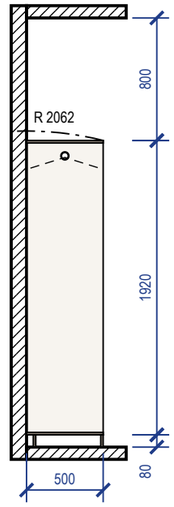

Разрез 2-2

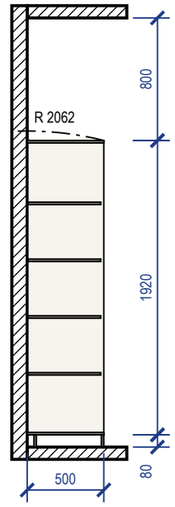


Примечания

1. Размеры — в мм по чистовой отделке; изделие 3000×500×2000 (Ш×Г×В). Перед раскроем — контрольный замер цеха после чистовой отделки стен, пола и потолка.
2. Корпус — ЛДСП 16 мм, задняя стенка ХДФ 4 мм в паз, цоколь 80 мм на регулируемых опорах; открытая система без фасадов, ящики с фасадами.
3. Кромка: скрытые торцы 0,4 мм, видимые 2 мм (ПВХ/АБС).
4. Номинальные зазоры: между фасадами ящиков 3 мм, фасад ящика — стойка 2 мм.
5. Ящики — направляющие полного выдвижения NL 450 (внутренняя глубина 496 мм ≥ NL + 3); присадка по 32-й системе — выполняет цех.
6. Зазор до потолка 800 мм.
7. Подъём корпуса: диагональ боковины $\sqrt{(2000^2 + 500^2)} = 2062$ мм < 2800 мм до потолка — корпус собирается лёжа и поднимается поворотом.
8. Крепление к стене от опрокидывания: true; основание стены и шаг анкеров — монтажная схема шкафов.


3D орто

					Проект: Дом 331 м²			
	Лист	№ док.	Подпись	Дата	Система хранения M_26	Стадия	Лист	Листов
Дизайнер	Кырлан А.С.			19.10.26		П	Д_4	155


Общий вид

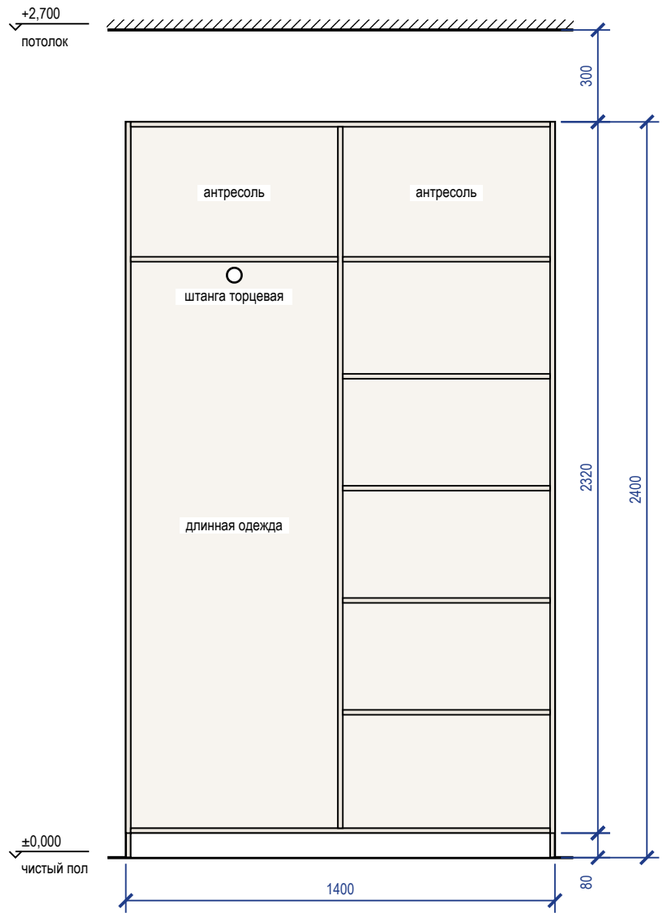


Наполнение, размеры в свету

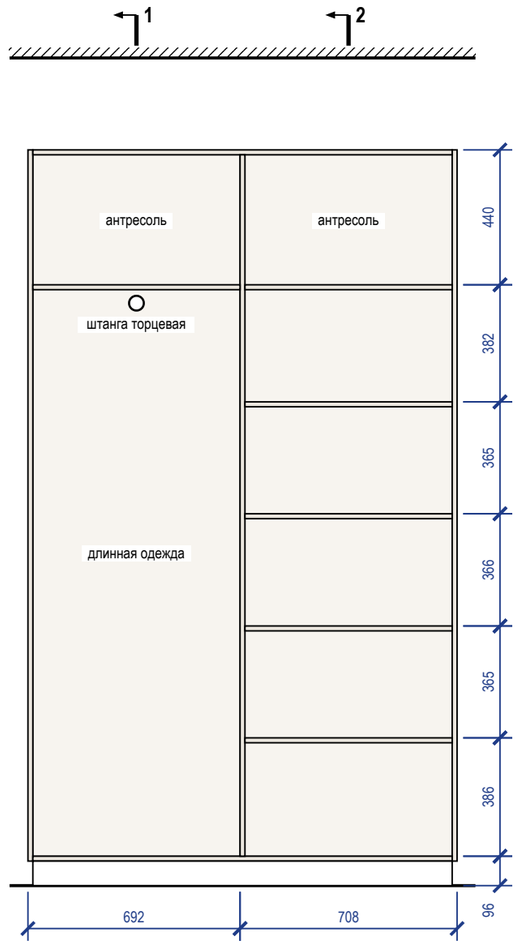

Разрез 1-1

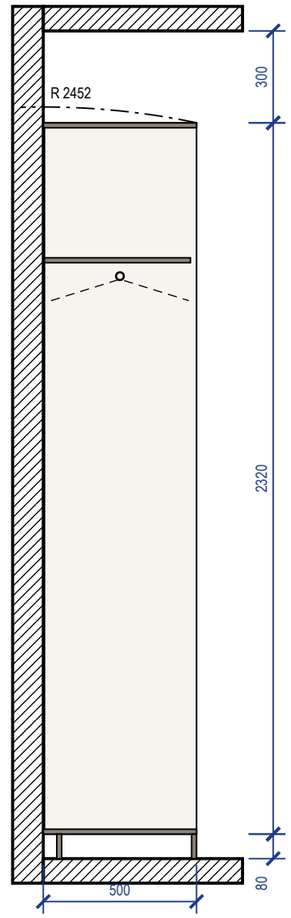


Разрез 2-2

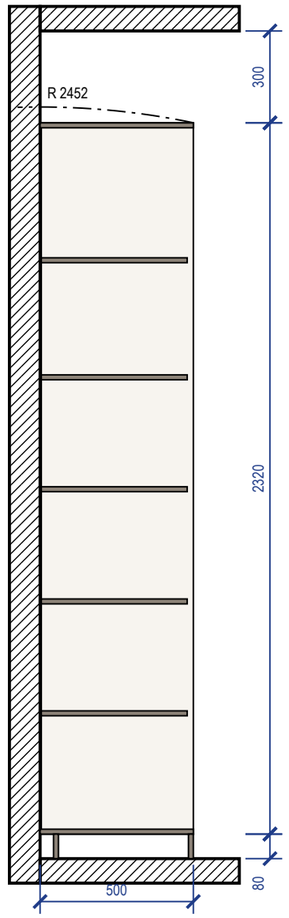

Примечания

1. Размеры — в мм по чистовой отделке; изделие 1400×500×2400 (Ш×Г×В). Перед раскроем — контрольный замер цеха после чистовой отделки стен, пола и потолка.
2. Корпус — ЛДСП 16 мм, задняя стенка ХДФ 4 мм в паз, цоколь 80 мм на регулируемых опорах; открытая система без фасадов, ящики с фасадами.
3. Кромка: скрытые торцы 0,4 мм, видимые 2 мм (ПВХ/АБС).
4. Номинальные зазоры: между фасадами ящиков 3 мм, фасад ящика — стойка 2 мм.
5. Ящики — направляющие полного выдвижения NL 450 (внутренняя глубина 496 мм ≥ NL + 3); присадка по 32-й системе — выполняет цех.
6. Зазор до потолка 300 мм.
7. Подъём корпуса: диагональ боковины $\sqrt{(2400^2 + 500^2)} = 2452$ мм < 2700 мм до потолка — корпус собирается лёжа и поднимается поворотом.
8. Крепление к стене от опрокидывания — уголки 2 шт. к несущему основанию (монтажная схема шкафов).

3D орто

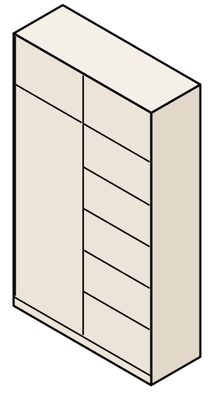


					Проект: Дом 331 м²
	Лист	№ док.	Подпись	Дата	Система хранения M_43
Дизайнер	Кырлан А.С.			19.10.26	


Стадия	Лист	Листов
П	Д_5	155

выпуск 18.10.2026 № ffc1f29499 · стр. 147 из 155


Вид с фасадами

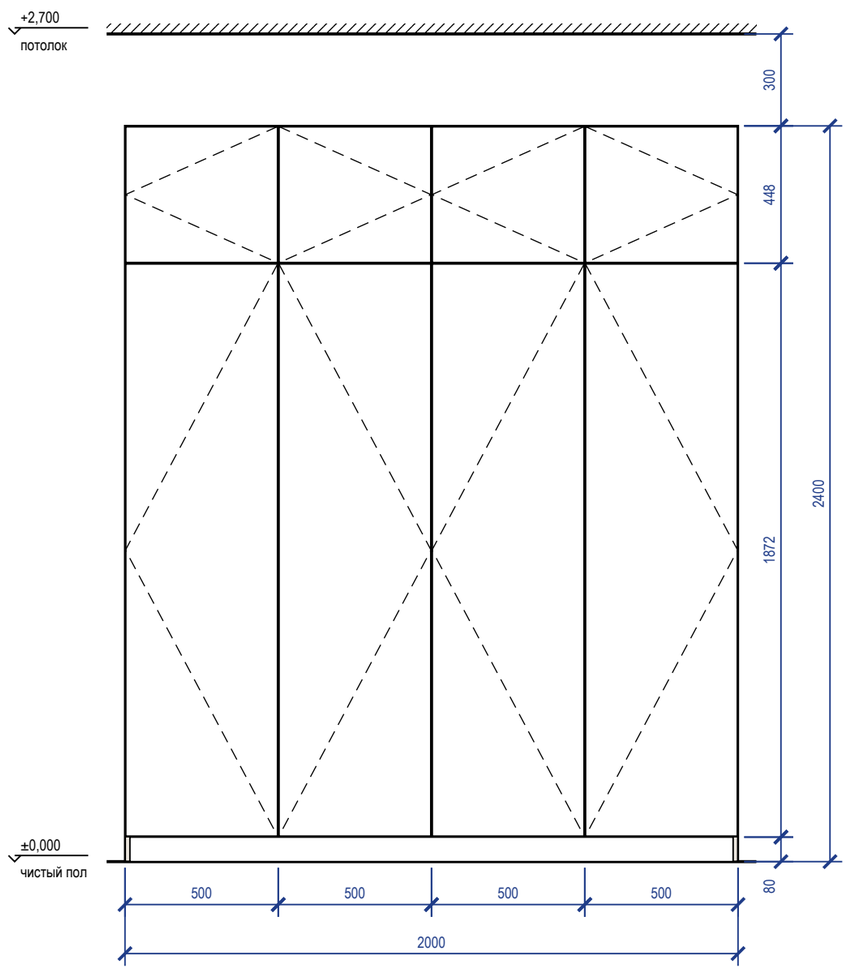


Вид без фасадов

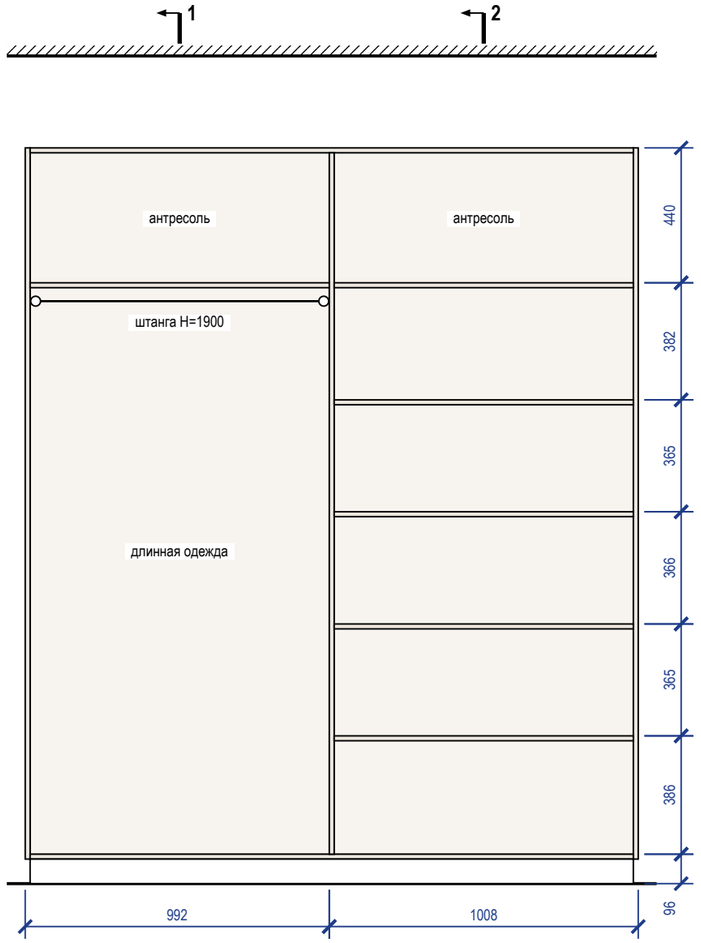

Разрез 1-1

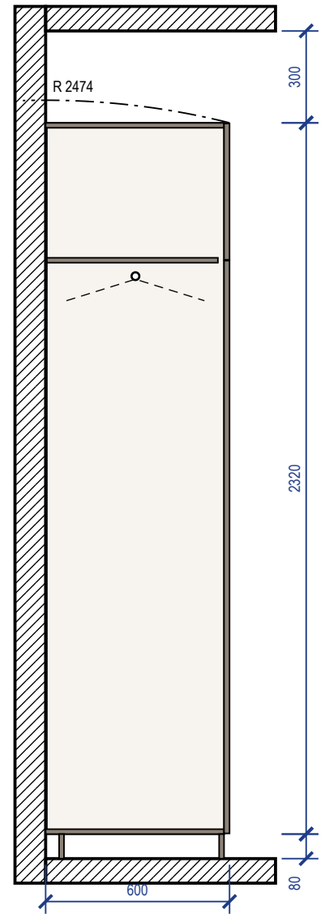


Разрез 2-2

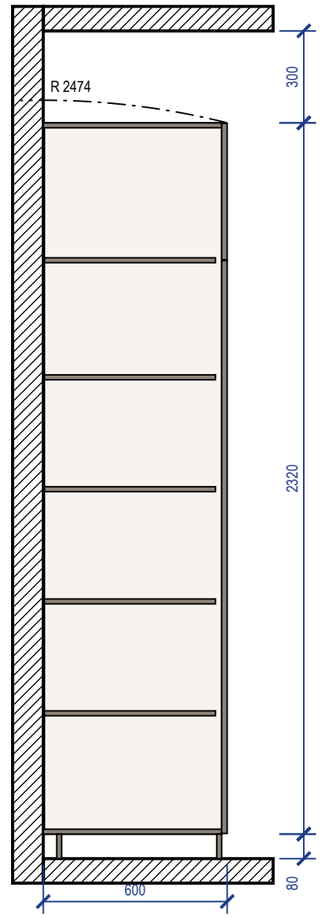

Примечания

1. Размеры — в мм по чистовой отделке; изделие 2000×600×2400 (Ш×Г×В). Перед раскроем — контрольный замер цеха после чистовой отделки стен, пола и потолка.
2. Корпус — ЛДСП 16 мм, задняя стенка ХДФ 4 мм в паз, цоколь 80 мм на регулируемых опорах; фасады — МДФ, эмаль матовая 18 мм накладные, цвет — по колерной карте; петли с доводчиком: фасад 1869 мм — 4 петли, фасад 445 мм — 2 петли.
3. Кромка: скрытые торцы 0,4 мм, видимые 2 мм (ПВХ/АБС).
4. Номинальные зазоры: между фасадами 3 мм, фасад — стена и фасад — потолок не менее 3 мм, фасад ящика — стойка 2 мм.
5. Ящики — направляющие полного выдвижения NL 550 (внутренняя глубина 578 мм ≥ NL + 3); присадка по 32-й системе — выполняет цех.
6. Зазор до потолка 300 мм.
7. Подъём корпуса: диагональ боковины $\sqrt{(2400^2 + 600^2)} = 2474$ мм < 2700 мм до потолка — корпус собирается лёжа и поднимается поворотом.
8. Крепление к стене от опрокидывания — уголки 2 шт. к несущему основанию (монтажная схема шкафов).


3D орто

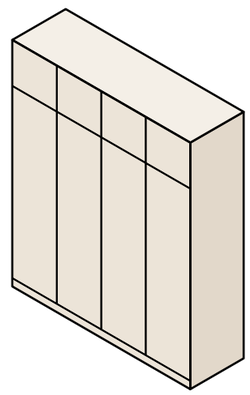


					Проект: Дом 331 м²	
	Лист	№ док.	Подпись	Дата	Шкаф распашной М_46	Стадия / Лист / Листов
Дизайнер	Кырлан А.С.			19.10.26		П / Д_6 / 155

выпуск 18.10.2026 № ffc1f29499 · стр. 148 из 155


Общий вид

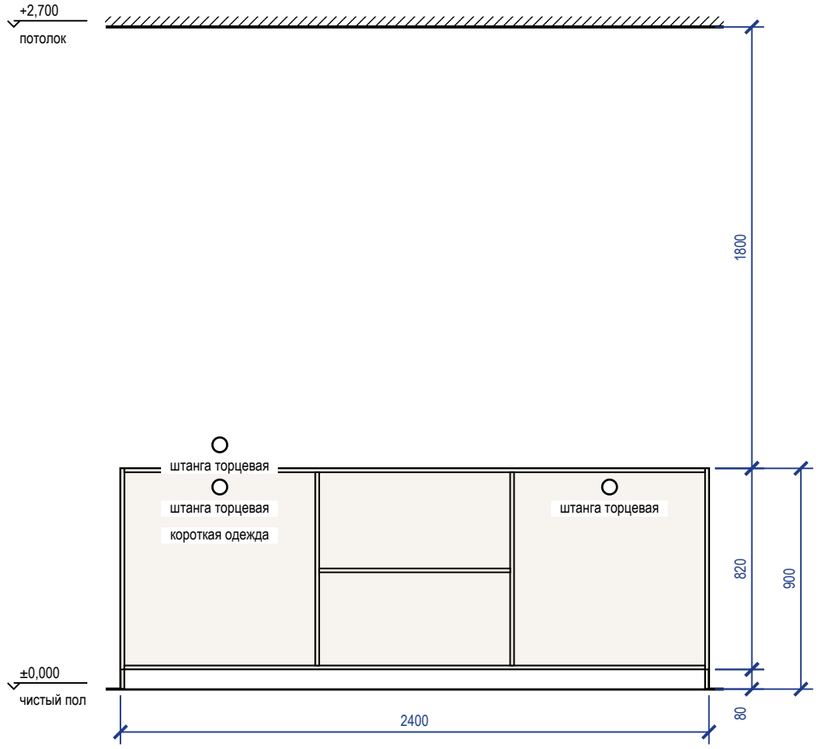


Наполнение, размеры в свету

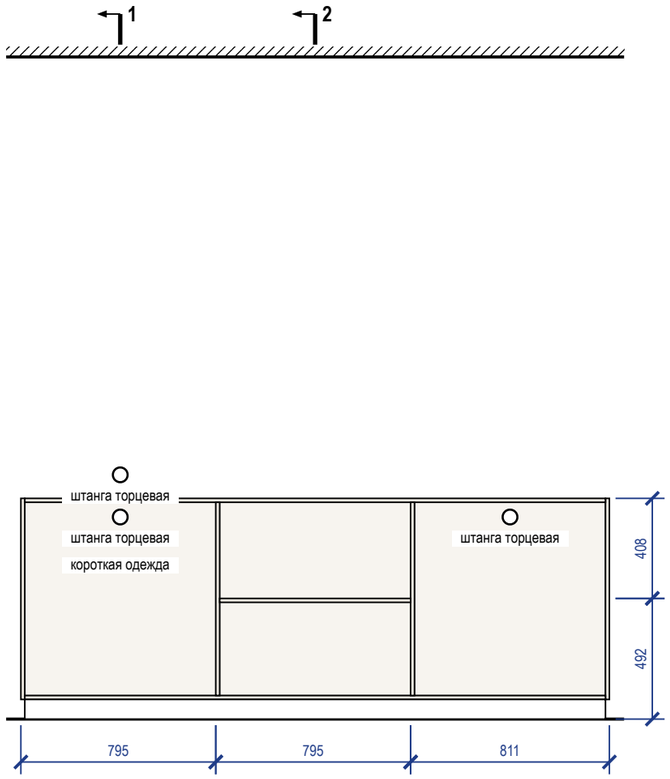

Разрез 1-1

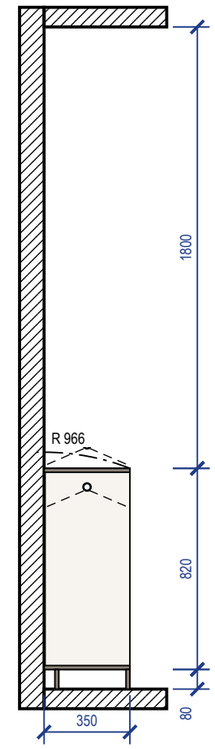


Разрез 2-2

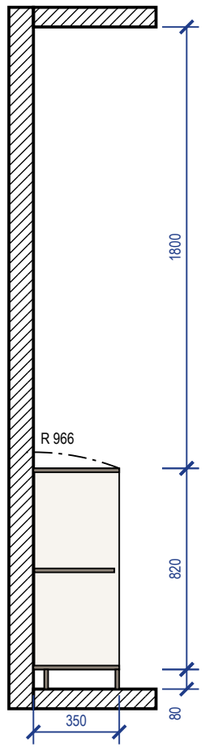

Примечания

1. Размеры — в мм по чистовой отделке; изделие 2400×350×900 (Ш×Г×В). Перед раскроем — контрольный замер цеха после чистовой отделки стен, пола и потолка.
2. Корпус — ЛДСП 16 мм, задняя стенка ХДФ 4 мм в паз, цоколь 80 мм на регулируемых опорах; открытая система без фасадов, ящики с фасадами.
3. Кромка: скрытые торцы 0,4 мм, видимые 2 мм (ПВХ/АБС).
4. Номинальные зазоры: между фасадами ящиков 3 мм, фасад ящика — стойка 2 мм.
5. Ящики — направляющие полного выдвижения NL 300 (внутренняя глубина 346 мм ≥ NL + 3); присадка по 32-й системе — выполняет цех.
6. Зазор до потолка 1800 мм.
7. Подъём корпуса: диагональ боковины $\sqrt{(900^2 + 350^2)} = 966$ мм < 2700 мм до потолка — корпус собирается лёжа и поднимается поворотом.
8. Крепление к стене от опрокидывания: true; основание стены и шаг анкеров — монтажная схема шкафов.

3D орто

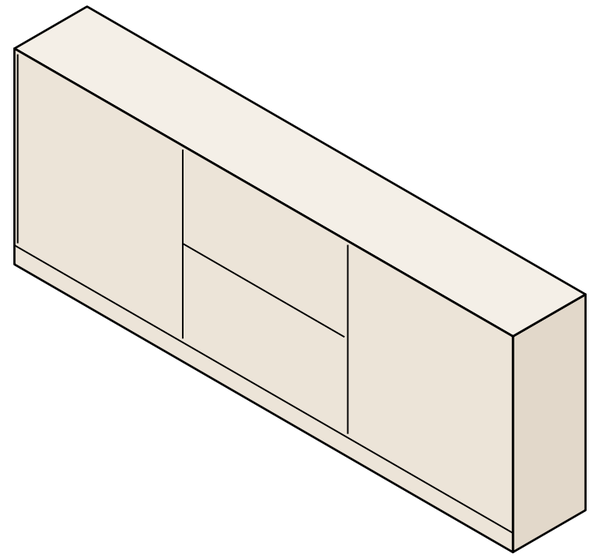


					Проект: Дом 331 м²
	Лист	№ док.	Подпись	Дата	Система хранения M_49
Дизайнер	Кырлан А.С.			19.10.26	


Стадия	Лист	Листов
П	Д_7	155

выпуск 18.10.2026 № ffc1f29499 · стр. 149 из 155


Вид с фасадами

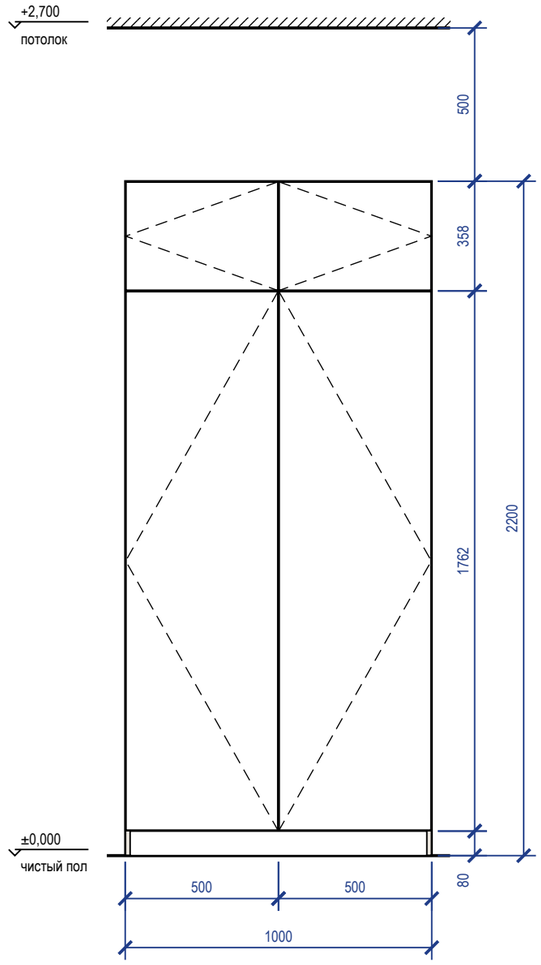

Вид без фасадов

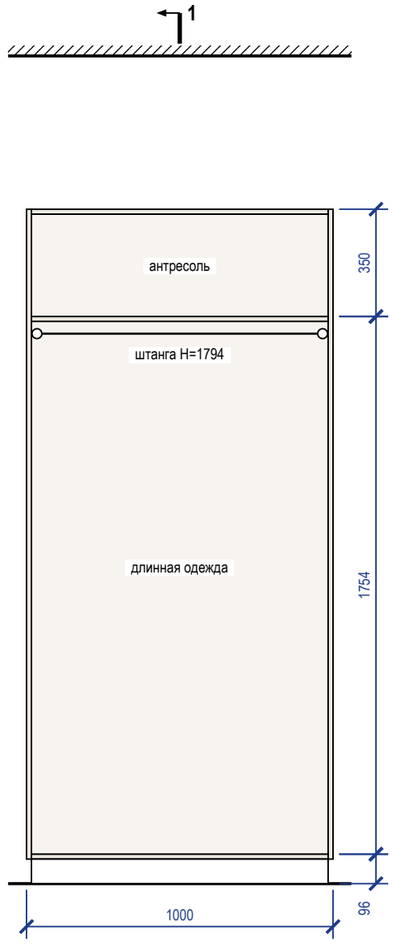


Разрез 1-1

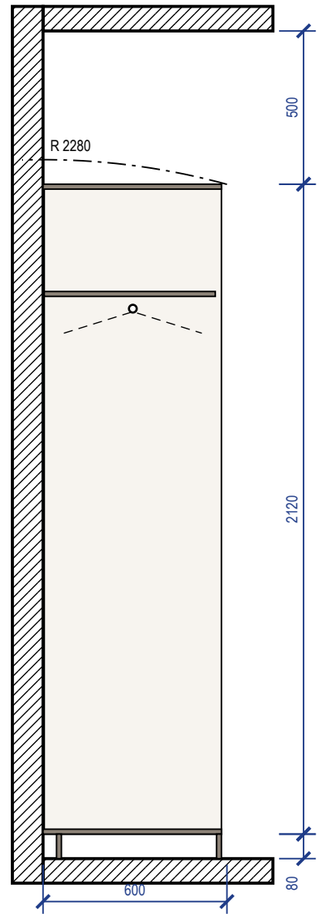

Примечания

1. Размеры — в мм по чистовой отделке; изделие 1000×600×2200 (Ш×Г×В). Перед раскроем — контрольный замер цеха после чистовой отделки стен, пола и потолка.
2. Корпус — ЛДСП 16 мм, задняя стенка ХДФ 4 мм в паз, цоколь 80 мм на регулируемых опорах; фасады — МДФ, эмаль матовая 18 мм накладные, цвет — по колерной карте; петли с доводчиком: фасад 1759 мм — 4 петли, фасад 355 мм — 2 петли.
3. Кромка: скрытые торцы 0,4 мм, видимые 2 мм (ПВХ/АБС).
4. Номинальные зазоры: между фасадами 3 мм, фасад — стена и фасад — потолок не менее 3 мм, фасад ящика — стойка 2 мм.
5. Ящики — направляющие полного выдвижения NL 550 (внутренняя глубина 578 мм ≥ NL + 3); присадка по 32-й системе — выполняет цех.
6. Зазор до потолка 500 мм.
7. Подъём корпуса: диагональ боковины $\sqrt{(2200^2 + 600^2)} = 2280$ мм < 2700 мм до потолка — корпус собирается лёжа и поднимается поворотом.
8. Крепление к стене от опрокидывания — уголки 2 шт. к несущему основанию (монтажная схема шкафов).

3D орто

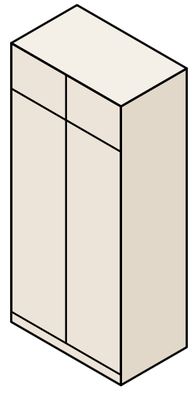


					Проект: Дом 331 м²
	Лист	№ док.	Подпись	Дата	Шкаф распашной М_53
Дизайнер	Кырлан А.С.			19.10.26	


Стадия	Лист	Листов
П	Д_8	155

выпуск 18.10.2026 № ffc1f29499 · стр. 150 из 155


Вид с фасадами

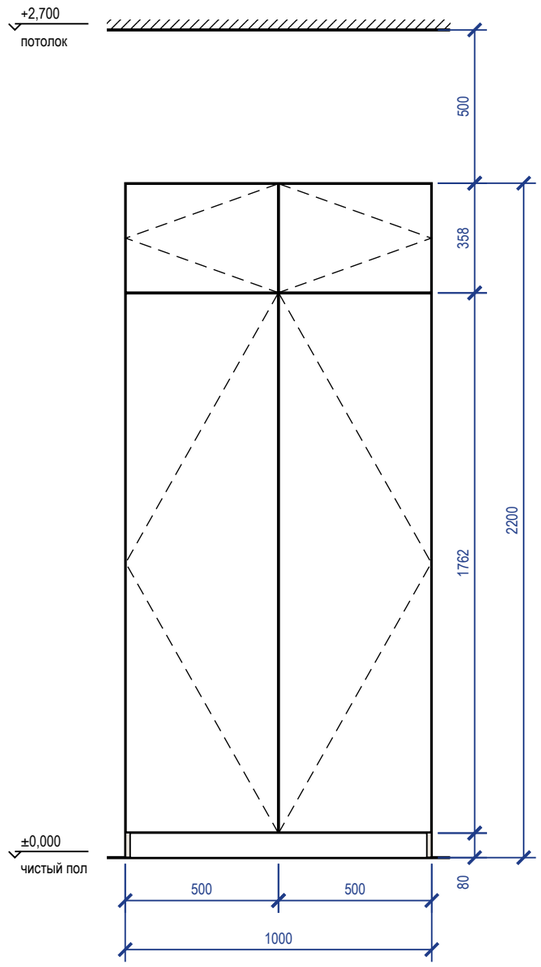

Вид без фасадов

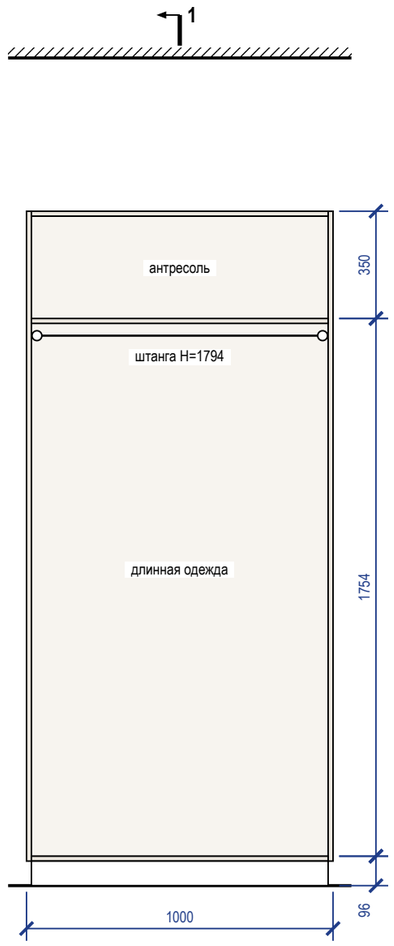


Разрез 1-1

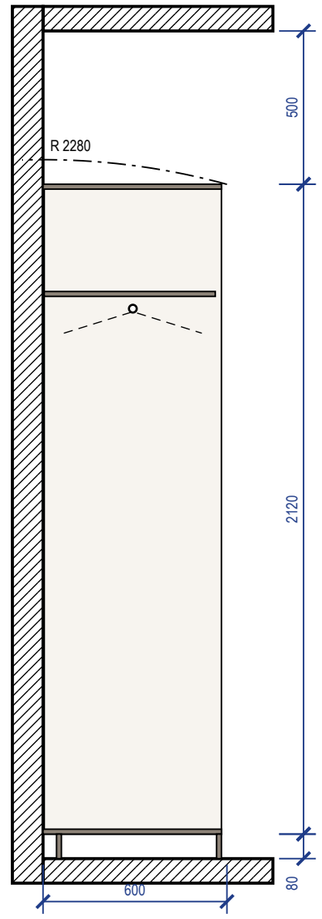

Примечания

1. Размеры — в мм по чистовой отделке; изделие 1000×600×2200 (Ш×Г×В). Перед раскроем — контрольный замер цеха после чистовой отделки стен, пола и потолка.
2. Корпус — ЛДСП 16 мм, задняя стенка ХДФ 4 мм в паз, цоколь 80 мм на регулируемых опорах; фасады — МДФ, эмаль матовая 18 мм накладные, цвет — по колерной карте; петли с доводчиком: фасад 1759 мм — 4 петли, фасад 355 мм — 2 петли.
3. Кромка: скрытые торцы 0,4 мм, видимые 2 мм (ПВХ/АБС).
4. Номинальные зазоры: между фасадами 3 мм, фасад — стена и фасад — потолок не менее 3 мм, фасад ящика — стойка 2 мм.
5. Ящики — направляющие полного выдвижения NL 550 (внутренняя глубина 578 мм ≥ NL + 3); присадка по 32-й системе — выполняет цех.
6. Зазор до потолка 500 мм.
7. Подъём корпуса: диагональ боковины $\sqrt{(2200^2 + 600^2)} = 2280$ мм < 2700 мм до потолка — корпус собирается лёжа и поднимается поворотом.
8. Крепление к стене от опрокидывания — уголки 2 шт. к несущему основанию (монтажная схема шкафов).


3D орто

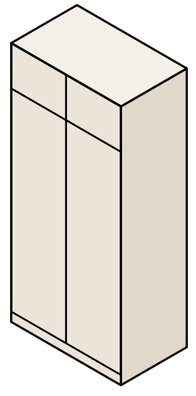


					Проект: Дом 331 м²	
	Лист	№ док.	Подпись	Дата	Шкаф распашной М_56	Стадия / Лист / Листов
Дизайнер	Кырлан А.С.			19.10.26		П / Д_9 / 155

выпуск 18.10.2026 № ffc1f29499 · стр. 151 из 155


Вид с фасадами

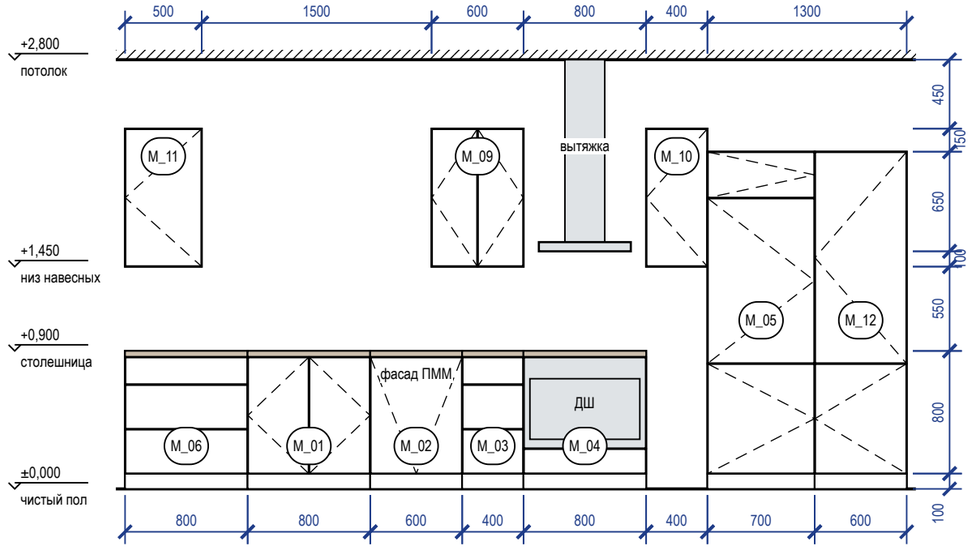


Вид без фасадов (наполнение, выводы)

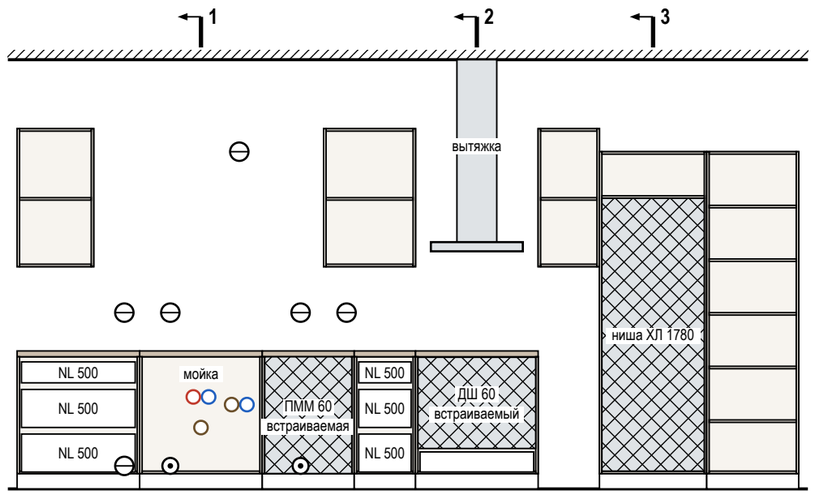


Разрез 1-1

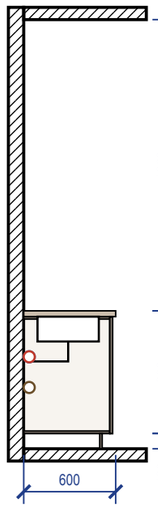


Разрез 2-2

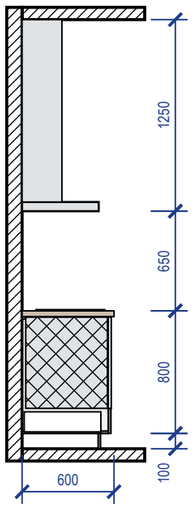

Разрез 3-3

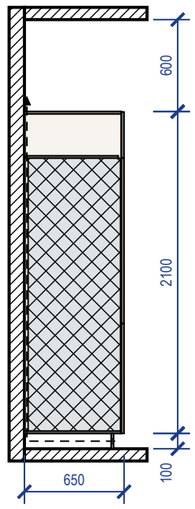

3D орто

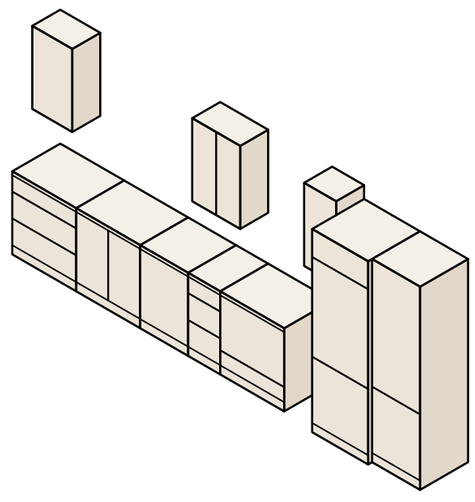

Примечания

1. Размеры — в мм по чистовой отделке, вид из помещения; марки — как на плане расстановки. Перед раскроем — контрольный замер цеха после фартука и пола.
2. Корпуса — ЛДСП 16 мм, задняя стенка ХДФ 4 мм; фасады — МДФ, эмаль матовая 18 мм, цвет по колерной карте; столешница 38 мм, свес 20 мм; цоколь 100 мм.
3. Кромка: скрытые торцы 0,4 мм, видимые 2 мм. Номинальные зазоры: между фасадами 3 мм, фасад — столешница 3 мм, фасад — стена не менее 3 мм.
4. Ящики полного выдвижения и петли — с доводчиком; присадка по 32-й системе — выполняет цех.
5. Низ вытяжки — не ниже 650 мм над варочной панелью или по паспорту модели; короб воздуховода — до потолка.
6. Ниши техники (холодильник — ориентир 1780 мм) — по монтажным схемам выбранных моделей: решётка в цоколе и канал за пеналом холодильника, зазор за духовым шкафом, фасад ПММ на двери машины.

					Проект: Дом 331 м²
	Лист	№ док.	Подпись	Дата	
Дизайнер	Кырлан А.С.			19.10.26	Кухня (пом. 1). Развёртка гарнитура

Стадия	Лист	Листов
П	Д_10	155

выпуск 18.10.2026 № ffc1f29499 · стр. 152 из 155

Ведомость отделки помещений (форма 1 прил. А ГОСТ 21.501-2018). Лист 1 из 3

№	Наименование помещения	Потолок			Стены и перегородки			Низ стен (плинтус)			Пол		Примечание
		Вид отделки	Код цвета	S, м²	Вид отделки	Код цвета	S, м²	Вид отделки	Код цвета	L, м	Вид отделки	S, м²	
1	Кухня-столовая 24,59 м²	Окраска, Tikkurila Luja 7, матовая, 2 слоя, подготовка Q3	NCS S 0804-Y30R	24,59	Окраска, Tikkurila Luja 7, полуматовая, 2 слоя, подготовка К3 Фартук кухни (стена А): облицовка керамогранитом, аналог: керамогранит матовый, тон F497, 600×600×9 мм, клей C2 TE S1, затирка CG2WA	NCS S 0804-Y30R #F1F1EC	47,03 0,93	Плинтус МДФ h=80 мм, аналог: МДФ под окраску 80×16 мм	NCS S 0804-Y30R	18,3	Инженерная доска, 1167-4250, 2100×127 мм, на клею; тип 1, отм. ЧП ±0,000	24,59	Н стен 2800 (до потолка); влагостойкая полуматовая окраска (класс мокрого истирания 1 по EN 13300); категория К3 по СП 71.13330.2017, табл. 7.5; по ГКЛ каркаса П113, влагостойкая окраска; Q3 колеруется в код стен, но по эмали на МДФ: сличать отдельным выкрасом на своей подложке (выкрас № 10); плинтус в цвет: стены
2	Кабинет-гостевая 11,92 м²	Окраска, Tikkurila Anti-Reflex 2, глубокоматовая, 2 слоя, подготовка Q3	Little Greene No. 105	11,92	Окраска, Farrow & Ball Modern Emulsion, матовая, 2 слоя, подготовка Q3 Акцент — стена А: окраска, Farrow & Ball Modern Emulsion, матовая, 2 слоя, подготовка Q3	Farrow & Ball No. 226 Farrow & Ball No. 298	26,42 5,96	Плинтус МДФ h=80 мм, аналог: МДФ под покраску 80×16	Farrow & Ball No. 226	11,7	Инженерная доска, 1167-4250, 2100×127 мм, на клею; тип 2, отм. ЧП ±0,000	11,92	Н стен 2800 (до потолка); плинтус в цвет: стены
3	Санузел 1 этажа 4,87 м²	Окраска, Tikkurila Luja 7, матовая, 2 слоя, подготовка Q3	Little Greene No. 105	4,87	Облицовка плиткой, A8UZ, 600×1200×9 мм, клей C2 TE S1, затирка CG2WA	Atlas Concorde A8UZ	20,53	нет			Керамогранит, A8UZ, 600×1200×9 мм; тип 3, отм. ЧП −0,015	4,87	Н стен 2815 (до потолка); гидроизоляция обмазочная, 2 слоя, с заведением на стены 200 мм (по пирогу пола); тест проливом и акт скрытых работ
4	Котельная 6,88 м²	Окраска, Tikkurila Anti-Reflex 2, глубокоматовая, 2 слоя, подготовка Q3	Little Greene No. 105	6,88	Окраска, Farrow & Ball Modern Emulsion, матовая, 2 слоя, подготовка Q3	Farrow & Ball No. 226	26,96	Плинтус МДФ h=80 мм, аналог: МДФ под покраску 80×16	Farrow & Ball No. 226	9,7	Керамогранит, A8UZ, 600×1200×9 мм; тип 4, отм. ЧП ±0,000	6,88	Н стен 2800 (до потолка); матовая моющаяся, класс 1 EN 13300 — осознанно вместо полуматовой; плинтус в цвет: стены
5	Гостиная 33,74 м²	Окраска, Tikkurila Anti-Reflex 2, глубокоматовая, 2 слоя, подготовка Q3	NCS S 0804-Y30R	33,74	Окраска, Tikkurila Optiva 5 Matt, матовая, 2 слоя, подготовка К3 Акцент — стена А: окраска, Tikkurila Optiva 5 Matt, матовая, 3 слоя, подготовка К3	NCS S 0804-Y30R Farrow & Ball No. 93	35,66 14,11	Плинтус МДФ h=80 мм, аналог: МДФ под окраску 80×16 мм	NCS S 0804-Y30R	18,2	Инженерная доска, 1167-4250, 2100×127 мм, на клею; тип 5, отм. ЧП ±0,000	33,74	Н стен 2800 (до потолка); колеруется в код стен, но по эмали на МДФ: сличать отдельным выкрасом на своей подложке (выкрас № 10); плинтус в цвет: стены
6	Холл с лестницей 10,02 м²	Окраска, Tikkurila Anti-Reflex 2, глубокоматовая, 2 слоя, подготовка Q3	Little Greene No. 105	10,02	Окраска, Farrow & Ball Modern Emulsion, матовая, 2 слоя, подготовка Q3	Farrow & Ball No. 226	23,56	Плинтус МДФ h=80 мм, аналог: МДФ под покраску 80×16	Farrow & Ball No. 226	7,0	Инженерная доска, 1167-4250, 2100×127 мм, на клею; тип 2, отм. ЧП ±0,000	10,02	Н стен 2800 (до потолка); матовая моющаяся, класс 1 EN 13300 — осознанно вместо полуматовой; плинтус в цвет: стены
7	Кладовая 5,99 м²	Окраска, Tikkurila Anti-Reflex 2, глубокоматовая, 2 слоя, подготовка Q3	Little Greene No. 105	5,99	Окраска, Tikkurila Harmony, матовая, 2 слоя, подготовка Q3	Little Greene No. 105	23,28	Плинтус МДФ h=80 мм, аналог: МДФ под покраску 80×16	Little Greene No. 105	7,8	Инженерная доска, 1167-4250, 2100×127 мм, на клею; тип 2, отм. ЧП ±0,000	5,99	Н стен 2800 (до потолка); плинтус в цвет: стены
8	Прихожая 12,46 м²	Окраска, Tikkurila Anti-Reflex 2, глубокоматовая, 2 слоя, подготовка Q3	Little Greene No. 105	12,46	Окраска, Farrow & Ball Modern Emulsion, матовая, 2 слоя, подготовка Q3	Farrow & Ball No. 226	40,71	Плинтус МДФ h=80 мм, аналог: МДФ под покраску 80×16	Farrow & Ball No. 226	13,6	Керамогранит, A8UZ, 600×1200×9 мм; тип 4, отм. ЧП ±0,000	12,46	Н стен 2800 (до потолка); матовая моющаяся, класс 1 EN 13300 — осознанно вместо полуматовой; плинтус в цвет: стены
9	Тамбур 3,49 м²	Окраска, Tikkurila Anti-Reflex 2, глубокоматовая, 2 слоя, подготовка Q3	Little Greene No. 105	3,49	Окраска, Farrow & Ball Modern Emulsion, матовая, 2 слоя, подготовка Q3	Farrow & Ball No. 226	17,07	Плинтус МДФ h=80 мм, аналог: МДФ под покраску 80×16	Farrow & Ball No. 226	5,6	Керамогранит, A8UZ, 600×1200×9 мм; тип 4, отм. ЧП ±0,000	3,49	Н стен 2800 (до потолка); матовая моющаяся, класс 1 EN 13300 — осознанно вместо полуматовой; плинтус в цвет: стены

Примечания

1. Ведомость продолжена на листе 2 из 3; итоги, сводка площадей и примечания — на последнем листе ведомости.

					Проект: Дом 331 м²
	Лист	№ док.	Подпись	Дата	Ведомость отделки помещений. Лист 1 из 3
Дизайнер	Кырлан А.С.			19.10.26	

Стадия	Лист	Листов
П	С1	155

выпуск 18.10.2026 № ffc1f29499 · стр. 153 из 155

Поз.	Наименование и техническая характеристика	Тип, марка, обозначение документа	Код продукции	Поставщик	Ед. изм.	Кол.	Образец	Примечание
	Лакокрасочные материалы							
1	Краска интерьерная водно-дисперсионная акриловая для стен, полуматовая, класс мокрого истирания 1 по EN 13300, база A; цвет NCS S 0804-Y30R «S 0804-Y30R», колеровка машинная	Tikkurila Luja 7		Tikkurila	л	31,5		поз. К1 колерной карты; пом. 1, 11, 12; S = 115,4 м² × 2 сл. × 0,12 л/м² = 27,7 л, +10 % и 0,5 л на подкраску → ≥ 31,0 л; тара 3 × 9 л + 1 × 2,7 л + 2 × 0,9 л
2	Краска интерьерная водно-дисперсионная акриловая для потолков, матовая, класс мокрого истирания 1 по EN 13300, база A; цвет NCS S 0804-Y30R «S 0804-Y30R», колеровка машинная	Tikkurila Luja 7		Tikkurila	л	14,4		поз. К2 колерной карты; пом. 1, 11, 12; S = 49,8 м² × 2 сл. × 0,12 л/м² = 12,0 л, +10 % и 0,5 л на подкраску → ≥ 13,6 л; тара 1 × 9 л + 2 × 2,7 л
3	Краска интерьерная водно-дисперсионная акриловая для стен, матовая, класс мокрого истирания 1 по EN 13300, база A; цвет Farrow & Ball No. 226 «Joa's White», колеровка машинная	Farrow & Ball Modern Emulsion		Farrow & Ball	л	92,5		поз. К4 колерной карты; пом. 2, 4, 6, 8, 9, 10, 13, 16, 17, 18, 19; S = 339,8 м² × 2 сл. × 0,12 л/м² = 81,6 л, +10 % и 0,5 л на подкраску → ≥ 90,2 л; тара 18 × 5 л + 1 × 2,5 л
4	Краска интерьерная водно-дисперсионная акриловая для акцентных стен, матовая, класс мокрого истирания 1 по EN 13300, база C; цвет Farrow & Ball No. 298 «Bancha», колеровка машинная	Farrow & Ball Modern Emulsion		Farrow & Ball	л	2,5		поз. К5 колерной карты; пом. 2; S = 6,0 м² × 2 сл. × 0,12 л/м² = 1,4 л, +10 % и 0,5 л на подкраску → ≥ 2,1 л; тара 1 × 2,5 л
5	Краска интерьерная водно-дисперсионная акриловая для потолков, глубокоматовая, класс мокрого истирания 2 по EN 13300, база A; цвет Little Greene No. 105 «Slaked Lime», колеровка машинная	Tikkurila Anti-Reflex 2		Tikkurila	л	54,9		поз. К6 колерной карты; пом. 2, 4, 6, 7, 8, 9, 10, 13, 14, 16, 17, 18, 19; S = 202,9 м² × 2 сл. × 0,12 л/м² = 48,7 л, +10 % и 0,5 л на подкраску → ≥ 54,1 л; тара 6 × 9 л + 1 × 0,9 л
6	Краска интерьерная водно-дисперсионная акриловая для потолков, матовая, класс мокрого истирания 1 по EN 13300, база A; цвет Little Greene No. 105 «Slaked Lime», колеровка машинная	Tikkurila Luja 7		Tikkurila	л	6,3		поз. К9 колерной карты; пом. 3, 15, 20; S = 20,9 м² × 2 сл. × 0,12 л/м² = 5,0 л, +10 % и 0,5 л на подкраску → ≥ 6,0 л; тара 2 × 2,7 л + 1 × 0,9 л
7	Краска интерьерная водно-дисперсионная акриловая для стен, матовая, класс мокрого истирания 2 по EN 13300, база A; цвет NCS S 0804-Y30R «S 0804-Y30R», колеровка машинная	Tikkurila Optiva 5 Matt		Tikkurila	л	10,8		поз. К10 колерной карты; пом. 5; S = 35,7 м² × 2 сл. × 0,12 л/м² = 8,6 л, +10 % и 0,5 л на подкраску → ≥ 9,9 л; тара 1 × 9 л + 2 × 0,9 л
8	Краска интерьерная водно-дисперсионная акриловая для акцентных стен, матовая, класс мокрого истирания 2 по EN 13300, база C; цвет Farrow & Ball No. 93 «Studio Green — почти чёрный зелёный», колеровка машинная	Tikkurila Optiva 5 Matt		Tikkurila	л	7,5		поз. К11 колерной карты; пом. 5; S = 14,1 м² × 3 сл. × 0,12 л/м² = 5,1 л, +10 % и 0,5 л на подкраску → ≥ 6,1 л; тара 1 × 5 л + 1 × 2,5 л
9	Краска интерьерная водно-дисперсионная акриловая для потолков, глубокоматовая, класс мокрого истирания 2 по EN 13300, база A; цвет NCS S 0804-Y30R «S 0804-Y30R», колеровка машинная	Tikkurila Anti-Reflex 2		Tikkurila	л	9,9		поз. К12 колерной карты; пом. 5; S = 33,7 м² × 2 сл. × 0,12 л/м² = 8,1 л, +10 % и 0,5 л на подкраску → ≥ 9,4 л; тара 1 × 9 л + 1 × 0,9 л
10	Краска интерьерная водно-дисперсионная акриловая для стен, матовая, класс мокрого истирания 1 по EN 13300, база A; цвет Little Greene No. 105 «Slaked Lime», колеровка машинная	Tikkurila Harmony		Tikkurila	л	11,7		поз. К13 колерной карты; пом. 7, 14; S = 42,0 м² × 2 сл. × 0,12 л/м² = 10,1 л, +10 % и 0,5 л на подкраску → ≥ 11,6 л; тара 1 × 9 л + 1 × 2,7 л
11	Краска интерьерная водно-дисперсионная акриловая для акцентных стен, матовая, класс мокрого истирания 1 по EN 13300, база C; цвет NCS S 7020-G10Y «Хвойный тёмно-зелёный», колеровка машинная	Farrow & Ball Modern Emulsion		Farrow & Ball	л	5		поз. К15 колерной карты; пом. 13; S = 8,0 м² × 2 сл. × 0,12 л/м² = 1,9 л, +10 % и 0,5 л на подкраску → ≥ 2,6 л; тара 1 × 5 л
12	Краска интерьерная водно-дисперсионная акриловая для акцентных стен, матовая, класс мокрого истирания 1 по EN 13300, база C; цвет Farrow & Ball No. 64 «Red Earth», колеровка машинная	Farrow & Ball Modern Emulsion		Farrow & Ball	л	5		поз. К16 колерной карты; пом. 16; S = 7,9 м² × 2 сл. × 0,12 л/м² = 1,9 л, +10 % и 0,5 л на подкраску → ≥ 2,6 л; тара 1 × 5 л
13	Краска интерьерная водно-дисперсионная акриловая для акцентных стен, матовая, класс мокрого истирания 1 по EN 13300, база C; цвет NCS S 3020-G30Y «S 3020-G30Y», колеровка машинная	Farrow & Ball Modern Emulsion		Farrow & Ball	л	5		поз. К17 колерной карты; пом. 18; S = 13,5 м² × 2 сл. × 0,12 л/м² = 3,2 л, +10 % и 0,5 л на подкраску → ≥ 4,1 л; тара 1 × 5 л
14	Краска интерьерная водно-дисперсионная акриловая для акцентных стен, матовая, класс мокрого истирания 1 по EN 13300, база C; цвет NCS S 3040-Y70R «S 3040-Y70R», колеровка машинная	Farrow & Ball Modern Emulsion		Farrow & Ball	л	5		поз. К19 колерной карты; пом. 19; S = 16,0 м² × 2 сл. × 0,12 л/м² = 3,8 л, +10 % и 0,5 л на подкраску → ≥ 4,7 л; тара 1 × 5 л
15	Акрилово-уретановая эмаль на водной основе, полуглянцевая в цвет NCS S 0804-Y30R «S 0804-Y30R» — окраска плинтуса	аналог по характеристикам			л	1		поз. К3; пом. 1, 5; L = 36,5 м, S = 3,5 м² × 2 сл. × 0,12 л/м² + 10 %; продукт подобрать в веере NCS
16	Краска для МДФ и дерева в цвет Farrow & Ball No. 226 «Joa's White» — окраска плинтуса; блеск не ниже блеска стен	марка не задана			л	3,2		поз. К7, К18; пом. 2, 4, 6, 8, 9, 13, 16, 17, 18, 19; L = 127,7 м, S = 11,9 м² × 2 сл. × 0,12 л/м² + 10 %; продукт подобрать в веере Farrow & Ball
17	Краска для МДФ и дерева в цвет Little Greene No. 105 «Slaked Lime» — окраска плинтуса; блеск не ниже блеска стен	марка не задана			л	0,5		поз. К14; пом. 7, 14; L = 16,8 м, S = 1,6 м² × 2 сл. × 0,12 л/м² + 10 %; продукт подобрать в веере Little Greene
18	Грунтовка акриловая под окраску стен и потолков — из системы производителя краски	по системе краски			м²	906		площадь окраски стен, акцентов и потолков; 1 слой перед окраской; расход — по ТУ грунтовки

	Лист	№ док.	Подпись	Дата	
Дизайнер	Кырлан А.С.			19.10.26	


Проект: Дом 331 м²

Спецификация отделочных материалов

Стадия	Лист	Листов
П	С2	155


1 Порог 15 мм: мокрая зона — жилое помещение (М 1:10)

Применение: двери Д-2, Д-9, Д-13

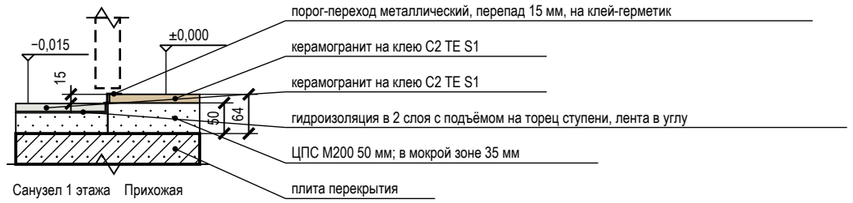


2 Стык покрытий пола Т-профилем без перепада (М 1:5)

Применение: проёмы 5↔11

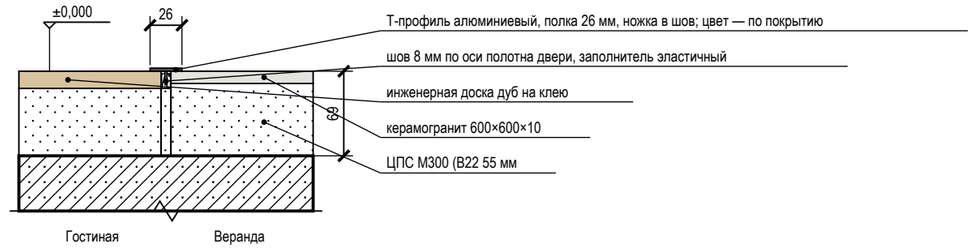


3 Дверь скрытого монтажа в плоскости стены, плинтус (М 1:5)

Применение: двери Д-1, Д-2, Д-7, Д-8, Д-9, Д-10, Д-11, Д-12, Д-13

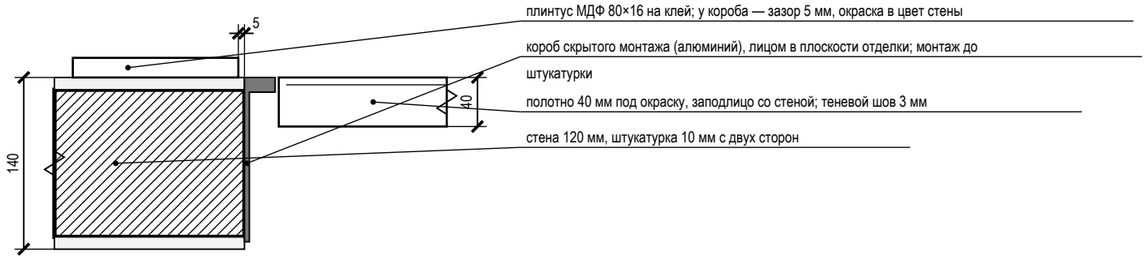


4 Короб стояков К1-1 с люком и звукоизоляцией (М 1:20)

Применение: пом. 3, 1, 8

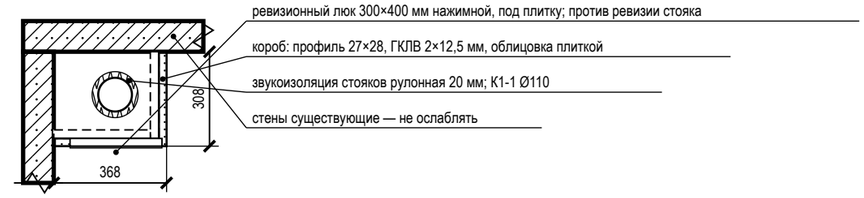


5 Гидроизоляция санузла: заход на стены 200 мм, примыкание ванны (М 1:20)

Применение: пом. 3, 15, 20

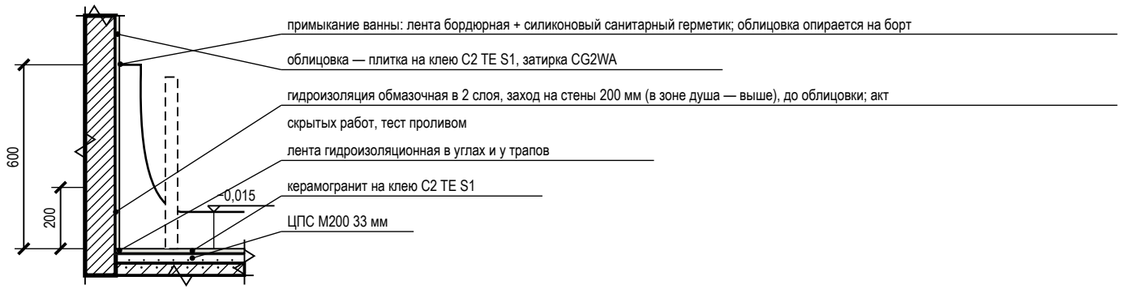

6 Плинтус МДФ 80×16 мм у окрашенной стены (М 1:10)

Применение: пом. 1, 2, 4, 5, 6, 7, 8, 9, 10, 13, 14, 16, 17, 18, 19

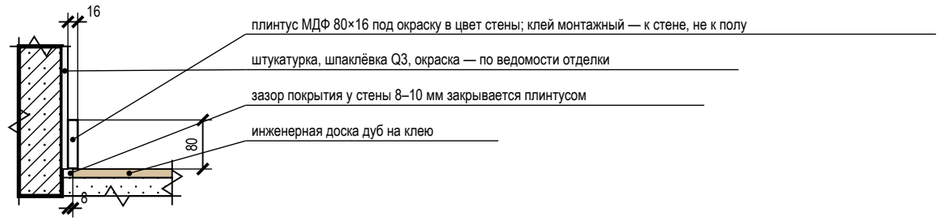

Условные обозначения

- железобетон (плита, стены)
- кладка, перегородка
- стяжка, раствор
- гипсокартон ГКЛВ
- звукоизоляция, эластичный заполнитель
- плитка, керамогранит на клею
- инженерная доска (покрытие пола)
- металлический профиль (порог, Т-профиль, короб двери)
- гидроизоляция (обмазочная, лента)

Примечания

1. Узлы — типовые решения проекта для мест, отмеченных выносками на листе схемы расположения развёрток и узлов; размеры — в мм, отметки — в м от ±0,000.
2. Узлы с гидроизоляцией, закладными и коробами скрытого монтажа принимаются по актам скрытых работ до закрытия отделкой; гидроизоляция — после теста проливом (24 ч).
3. Марки изделий (порог, Т-профиль, короб скрытой двери, люк) — по спецификациям; замена — на аналог с теми же габаритами по согласованию с автором проекта.

					Проект: Дом 331 м²
	Лист	№ док.	Подпись	Дата	Узлы
Дизайнер	Кырлан А.С.			19.10.26	

Стадия	Лист	Листов
П	С3	155

выпуск 18.10.2026 № ffc1f29499 · стр. 155 из 155