ДИЗАЙН-ПРОЕКТ ИНТЕРЬЕРА

Квартира 56 м²

джапанди

56,37 м²

тишина · заземлённость · медленная жизнь · тёплый минимализм · ваби-саби · hygge

Джапанди по брифу: стены S 0804-Y30R, потолок Damask F485, серо-зелёный Sea Smoke и дуб под маслом, акценты олива Bancha и тёмный орех; без глянца.

ПАЛИТРА 60 / 30 / 10

NCS S 0804-Y30R	F485	Little Greene No. 105	X447	V484
60 %	60 %	60 %	30 %	30 %

АВТОР ПРОЕКТА

Кырлан Александр Сергеевич

Октябрь 2026

место под визуализацию: вид сверху (3D) с мебелью, текстилем и декором

Визуализация «вид сверху» — в работе

ОБЪЕКТ	ОБЩАЯ ПЛОЩАДЬ	ПОМЕЩЕНИЙ
Квартира 56 м²	56,37 м²	5, из них жилых 3
СТИЛЬ	**СТАДИЯ**	**ШИФР**
Джапанди	Рабочий проект	ГД-2026-011-АИ

					Проект: Квартира 56 м²			
	Лист	№ док.	Подпись	Дата	Титульный лист	Стадия	Лист	Листов
Дизайнер	Кырлан А.С.			19.10.26		П	1	56

выпуск 19.10.2026 № 60226ce68e · стр. 1 из 56

Список листов

Лист	Наименование
1	Титульный лист
2	Список листов
3	План планировки от заказчика
4	План монтажный
5	Схема каркаса перегородки П-2
6	Кухня (пом. 1). Монтажная схема
7	Шкафы. Монтажная схема
8	Карта покрытий стен
9	Колерная карта
10	План размещения мебели и оборудования
11	Спецификация мебели и оборудования
12	Спецификация мебели и оборудования (продолжение)
13	Ведомости изделий, техники и фурнитуры
14	План выводов сантехники
15	Схема разводки водопровода и канализации
16	Спецификация сантехнического оборудования
17	Раскладка плитки. Санузел. Развёртки стен
18	План размещения дверей
19	План потолков
20	Разрезы и узлы потолков
21	План розеток и электровыводов
22	План слаботочных сетей
23	План освещения
24	Спецификация светильников и сценарии освещения
25	Управление светильниками
26	План вентиляции
27	План отопления
28	План покрытий пола
29	Раскладка плитки. Планы полов
30	Раскладка плитки. Прихожая. Фартук кухни
31	Развёртка стены Г. Гостиная-кухня (пом. 1), кухонный фронт
32	Развёртка стены А. Гостиная-кухня (пом. 1)
33	Развёртка стены Б. Гостиная-кухня (пом. 1)
34	Развёртка стены В. Гостиная-кухня (пом. 1)
35	Развёртка стены А. Спальня (пом. 2)
36	Развёртка стены Б. Спальня (пом. 2)
37	Развёртка стены В. Спальня (пом. 2)
38	Развёртка стены Г. Спальня (пом. 2)
39	Развёртка стены А. Детская (пом. 3)
40	Развёртка стены Б. Детская (пом. 3)

Лист	Наименование
41	Развёртка стены В. Детская (пом. 3)
42	Развёртка стены Г. Детская (пом. 3)
43	Развёртки стен А, Б. Санузел (пом. 4)
44	Развёртки стен В, Г. Санузел (пом. 4)
45	Развёртка стены А. Прихожая (пом. 5)
46	Развёртка стены Б. Прихожая (пом. 5)
47	Развёртка стены В. Прихожая (пом. 5)
48	Развёртка стены Г. Прихожая (пом. 5)
Д_1	Шкаф распашной М_19
Д_2	Шкаф распашной М_23
Д_3	Шкаф-купе М_27
Д_4	Система хранения М_29
Д_5	Кухня (пом. 1). Развёртка гарнитура
С1	Ведомость отделки помещений
С2	Спецификация отделочных материалов
С3	Узлы


Общие указания

1. Размеры даны в мм от чистовых поверхностей стен: слой штукатурки 20 мм по блоку и 5 мм шпаклёвки по ГКЛ учтён. Перед заказом встроенной мебели — контрольный обмер после штукатурки.
2. Привязки мебели — от стен и углов помещения, а не от другой мебели.
3. Розетки, выводы и выключатели под мебель — см. лист 21 «План розеток и электровыводов»; сантехприборы и выводы воды — лист 14.
4. План расстановки не является документацией для изготовления мебели: изделия — по чертежам мебельщика; покупную мебель заменять только на изделия не больше габарита из спецификации (лист 11).
5. Встроенная мебель «стена в стену» — с зазором 10 мм с каждой стороны или с компенсаторами.
6. Развёртки — вид на стену изнутри помещения, по часовой стрелке; расположение стен на схеме листа развёртки; размеры — в мм по чистовым поверхностям; отметки — в м от ±0,000; высоты Н — от чистого пола помещения до оси изделия, у декора — до центра.
7. Красные цепочки — привязки электроточек и выводов: по горизонтали от угла чистовых стен, по вертикали от чистого пола, до оси изделия; звенья короче 3 мм на листе вынесены во второй ярус (ближняя к стене цепочка).
8. У знака электроточки: марка (Р — розетка, S — выключатель, Св — светильник, ЭВ вывод кабеля), ×N — число постов в рамке, гр. — группа щита, Н — высота оси от чистого пола, мм; группы по клавишам выключателя — на листе выключателей.
9. Схема мебели, приборов и декора не является технической документацией для производства мебели; габариты — по паспортам изделий.
10. Марки позиций: М_NN — мебель, ОБ_NN — оборудование, С_NN — сантехника; О-N отделка (ведомость отделочных материалов, серия С).
11. Размеры мебели и изделий на заказ уточнить по месту после отделочных работ.

					Проект: Квартира 56 м²
	Лист	№ док.	Подпись	Дата	
Дизайнер	Кырлан А.С.			19.10.26	Список листов

Стадия	Лист	Листов
П	2	56

выпуск 19.10.2026 № 60226ce68e · стр. 2 из 56

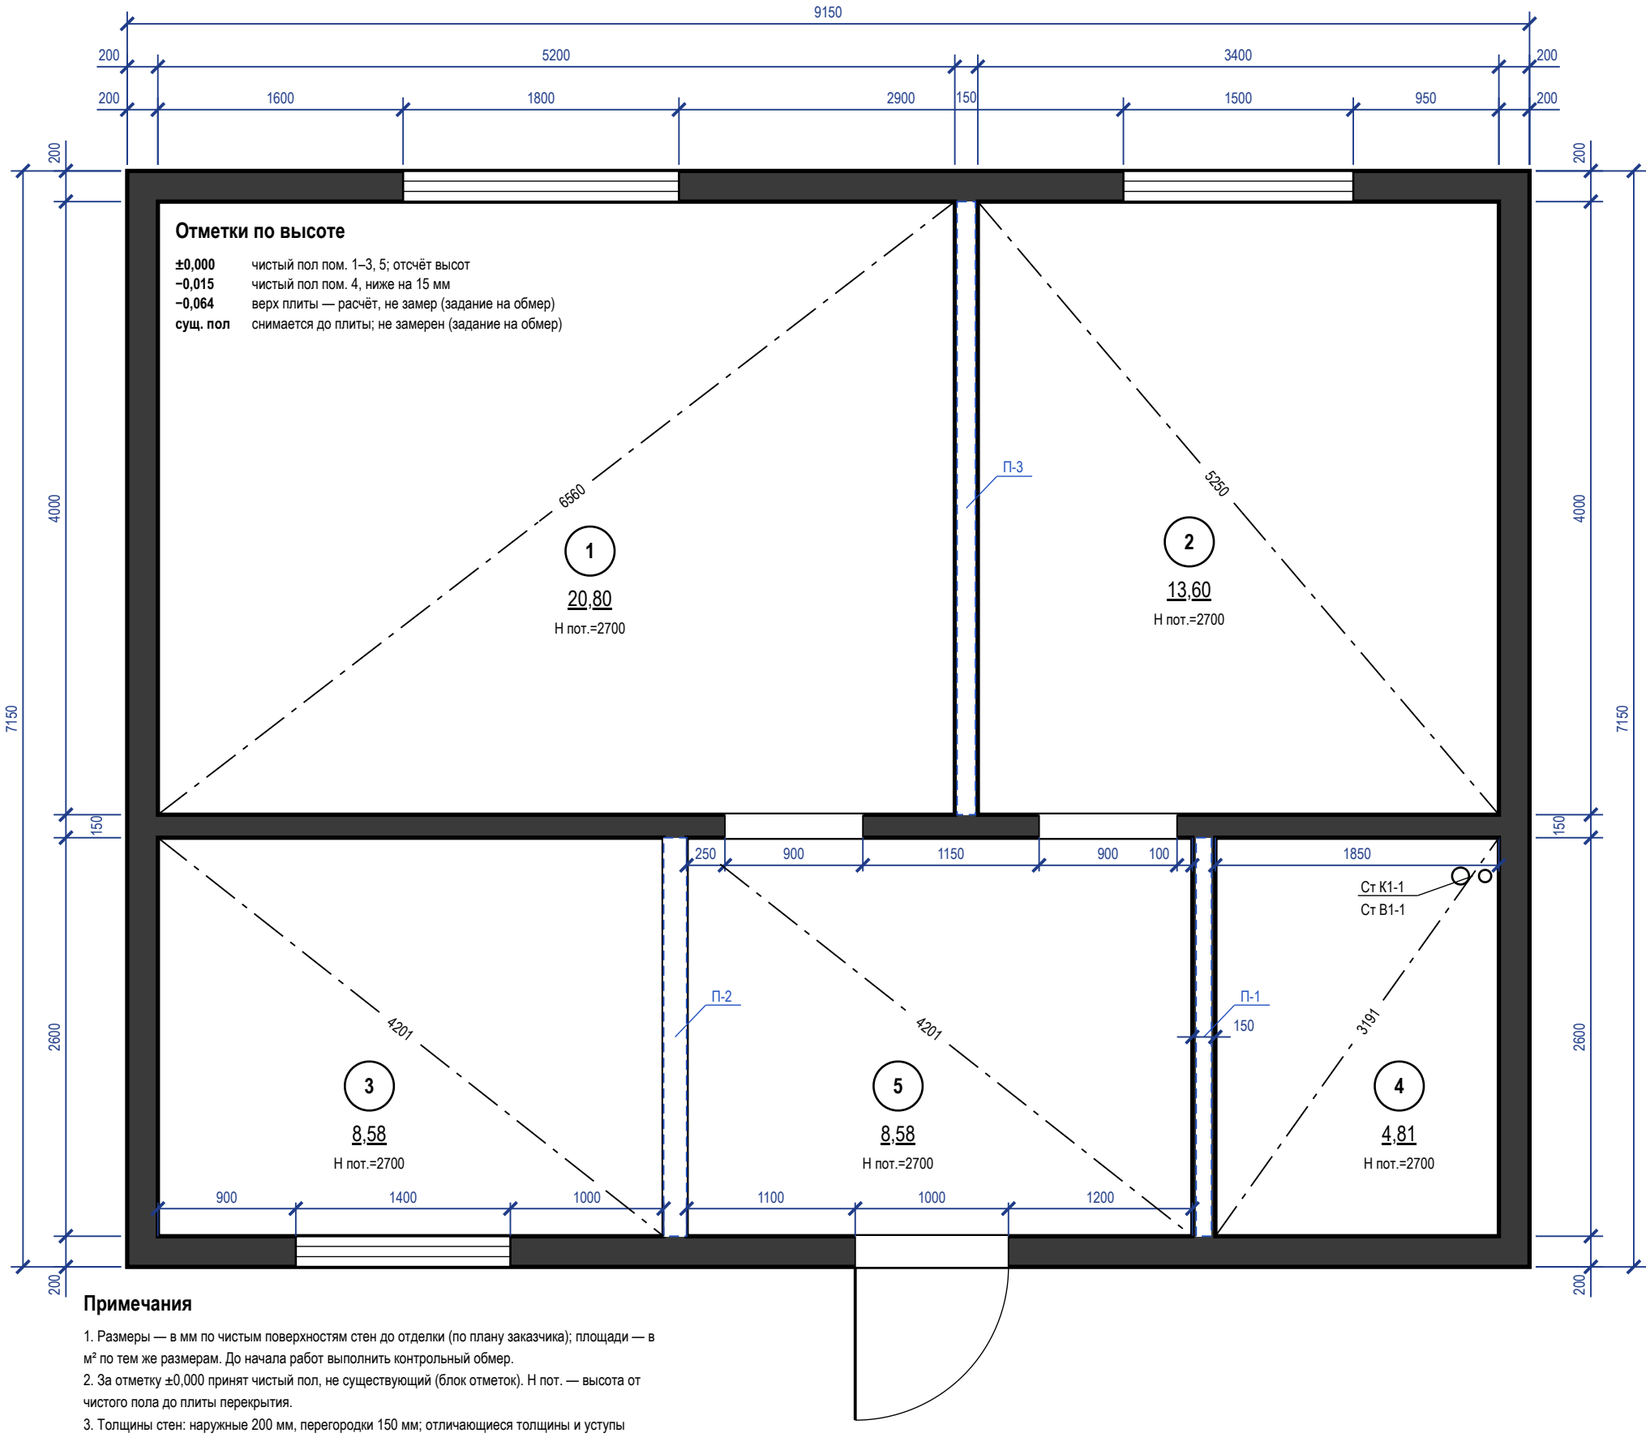

Экспликация помещений

№	Наименование	Площадь, м²
1	Гостиная-кухня	20,80
2	Спальня	13,60
3	Детская	8,58
4	Санузел	4,81
5	Прихожая	8,58
	Итого (общая площадь)	**56,37**

Условные обозначения

- существующие стены (сечение)
- окно (рама, остекление)
- проём существующий, без заполнения (откосы)
- стояк: К1 — канализация, В1 — ХВС, Т3 — ГВС
- проектная конструкция — на объекте её нет (контур)
- диагональ помещения — контроль прямоугольности
- (1) номер помещения, площадь м²

Примечания

1. Размеры — в мм по чистым поверхностям стен до отделки (по плану заказчика); площади — в м² по тем же размерам. До начала работ выполнить контрольный обмер.
2. За отметку ±0,000 принят чистый пол, не существующий (блок отметок). Н пот. — высота от чистого пола до плиты перекрытия.
3. Толщины стен: наружные 200 мм, перегородки 150 мм; отличающиеся толщины и уступы размерами на плане.
4. Несущие стены не определены: до технического заключения все стены считать несущими; проёмы и штробы в них не выполнять.
5. Дверные проёмы показаны без заполнения (двери — лист 18); высота дверных проёмов 2100 мм; низ окон (подоконник) 850, 900 мм от чистого пола, высота окон 1500, 1450 мм.
6. Диагонали — контрольные размеры; расхождение более 5 мм подписать на плане как перекос.
7. Размеры проверить на месте до начала работ; расхождение контрольных промеров ≤ 2 %.


					Проект: Квартира 56 м²
	Лист	№ док.	Подпись	Дата	
Дизайнер	Кырлан А.С.			19.10.26	План планировки от заказчика

Стадия	Лист	Листов
П	3	56

выпуск 19.10.2026 № 60226ce68e · стр. 3 из 56

Экспликация помещений

№	Наименование	Площадь, м²
1	Гостиная-кухня	20,80
2	Спальня	13,60
3	Детская	8,58
4	Санузел	4,81
5	Прихожая	8,58
	Итого (общая площадь)	**56,37**

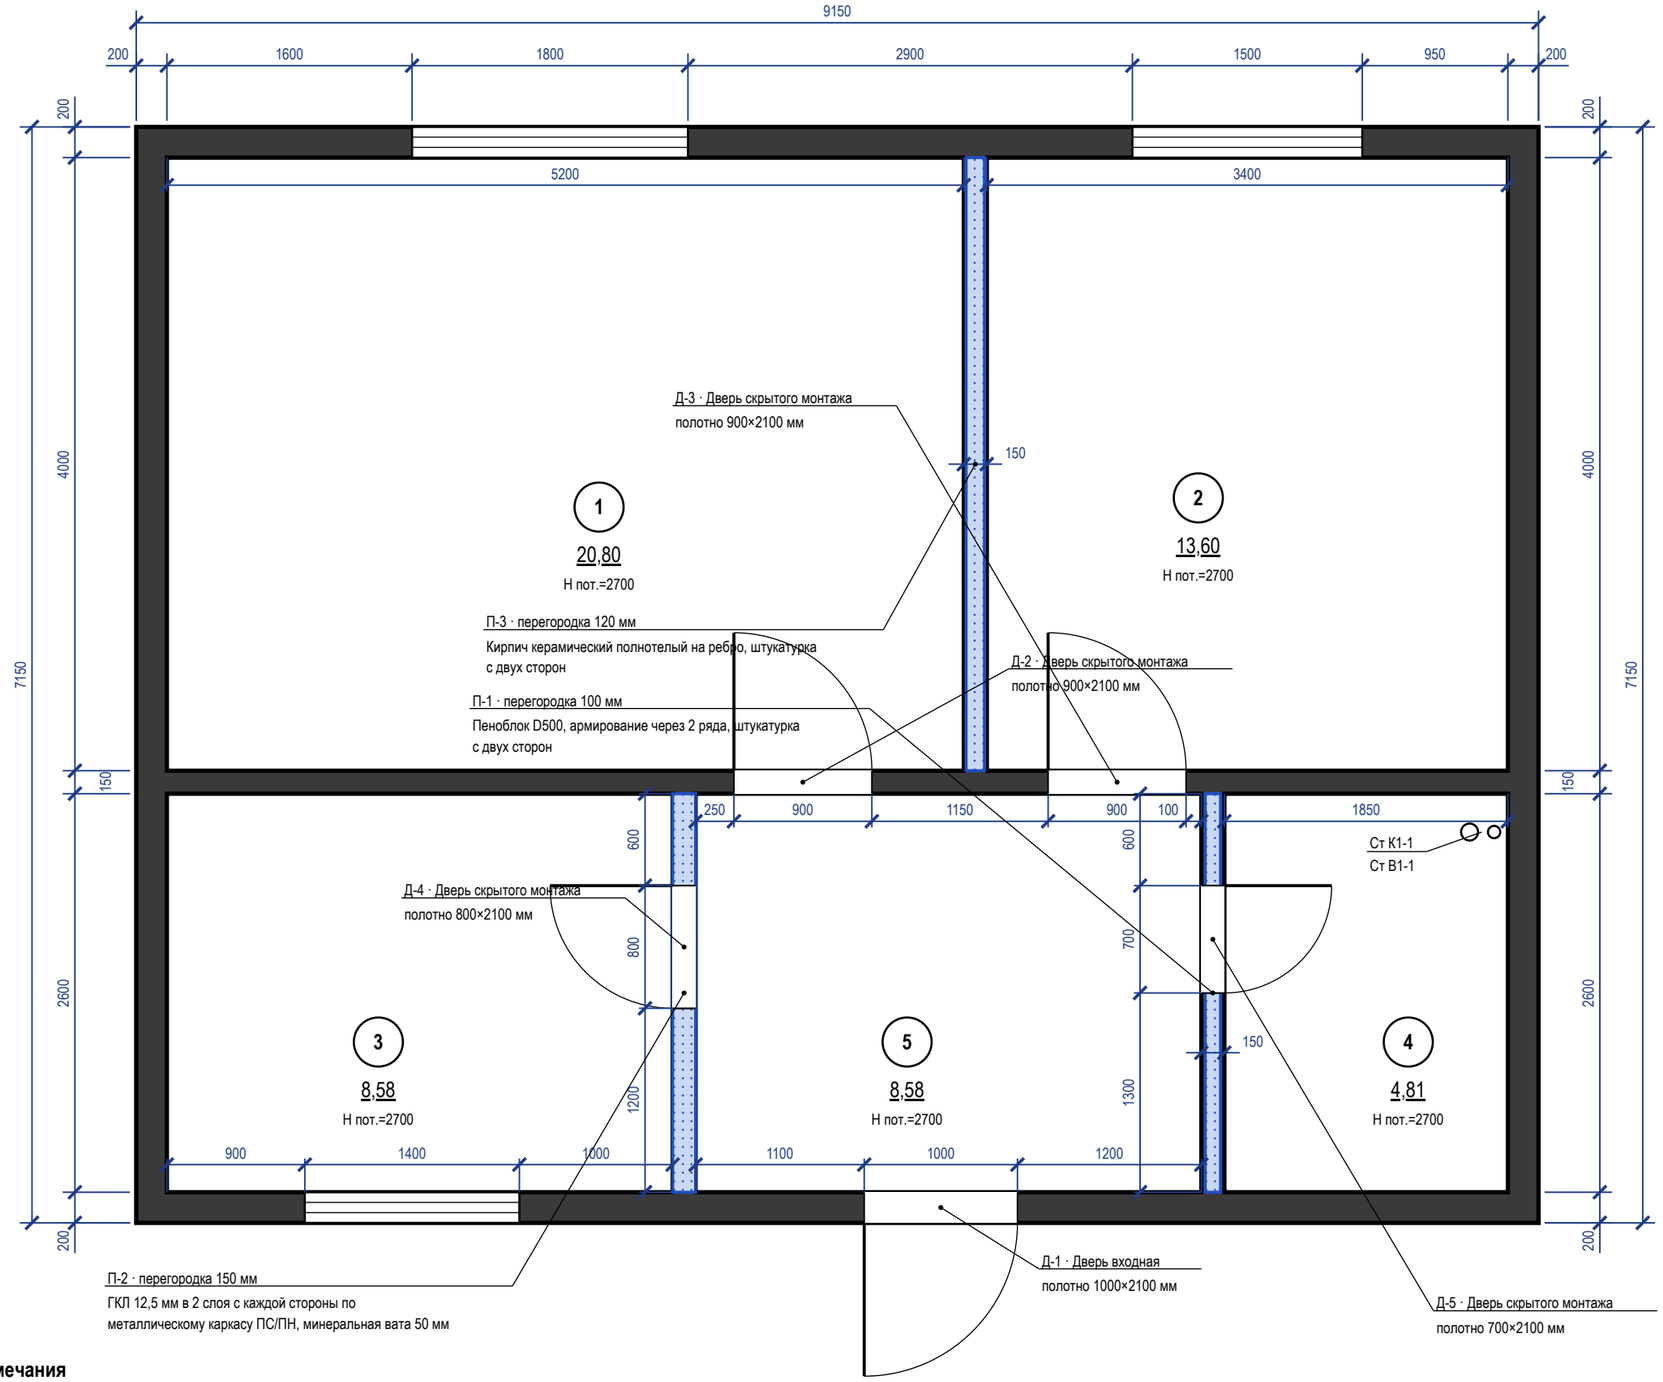

Примечания


1. Размеры — в мм от чистовых поверхностей стен до отделки; размеры уточнить по месту до начала работ.
2. Новые перегородки и облицовки — синим; каркас и обшивка — по выноскам; двери и проёмы лист 18.
3. Несущие стены не изменять: проёмы, ниши и штробы в них — только по техническому заключению.

					Проект: Квартира 56 м²
	Лист	№ док.	Подпись	Дата	План монтажный
Дизайнер	Кырлан А.С.			19.10.26	

Стадия	Лист	Листов
П	4	56

выпуск 19.10.2026 № 60226ce68e · стр. 4 из 56


Вид на каркас без обшивки (М 1:25)

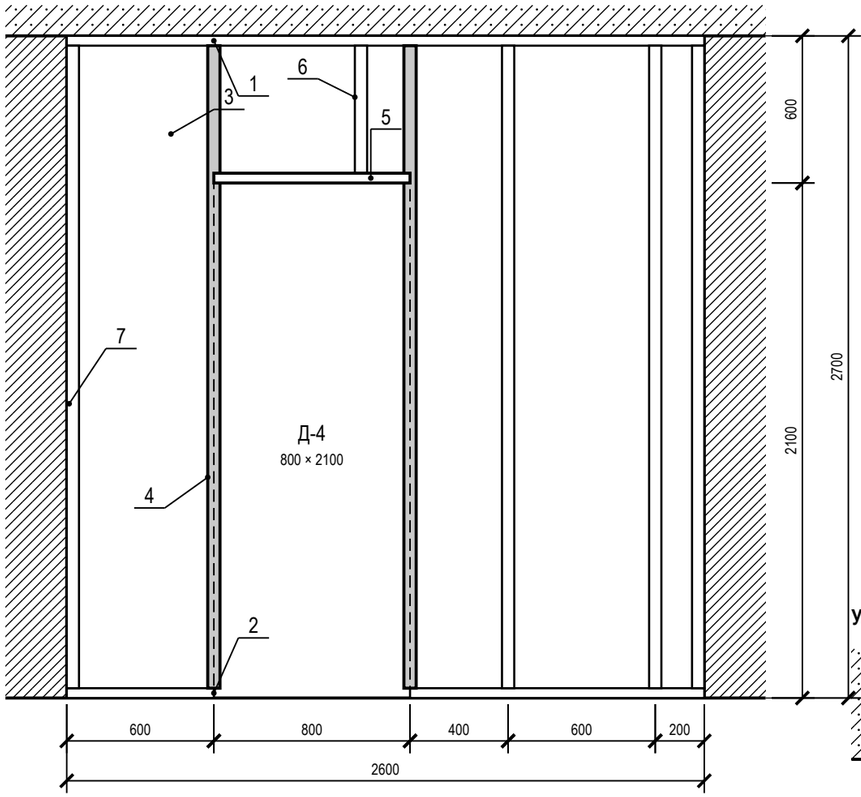

Оси — стойки каркаса; полки профиля на виде условны

Сечение А–А по стойке (М 1:5)


сверху — пом. 3, окраска

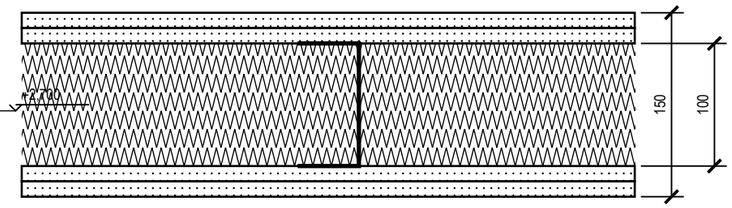

снизу — пом. 5, окраска

поз. 9 — ГКЛ 12,5 мм в 2 слоя с каждой стороны; поз. 3 — ПС 100; поз. 8 — минвата 100 мм (принято)

Сечение Б–Б у проёма, на уровне ниже перемычки (М 1:5)

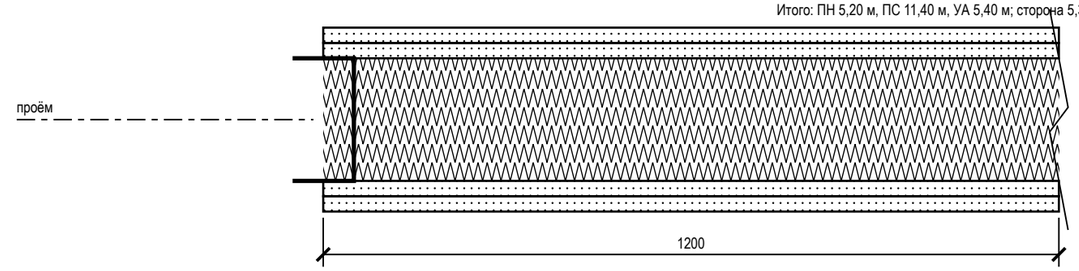


поз. 4 — УА 100, обрамление проёма; обшивка по краю проёма, простенок 1200 мм до пилона (на сечении показан с обрывом)

Ведомость элементов каркаса


Поз.	Наименование	Кол-во	Ед.
1	ПН 100 по потолку (по плите)	2,60	м
2	ПН 100 по полу, без проёма	1,80	м
3	ПС 100 через 600 мм	4 × 2,70	м
4	УА 100 по краям проёма	2 × 2,70	м
5	ПН 100 перемычка над проёмом	0,80	м
6	ПС 100 над перемычкой	1 × 0,60	м
7	Лента уплотнительная под профили	9,80	м
8	Минвата в полость, 100 мм	5,34	м²
9	ГКЛ 12,5 мм, 2 слоя с двух сторон	21,36	м²

Итого: ПН 5,20 м, ПС 11,40 м, УА 5,40 м; сторона 5,34 м²

Узел 1. К плите (М 1:5)

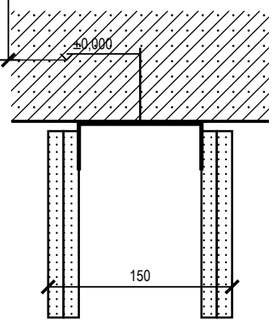

Узел 2. К полу (М 1:5)

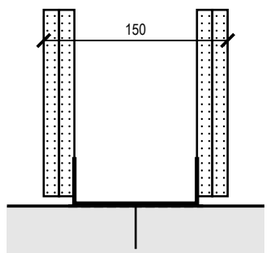

Примечания


1. П-2 (С112, ГКЛ в 2 слоя с каждой стороны, толщина 150 мм, высота 2700 мм до плиты); ось и длина 2600 мм — со скана плана заказчика (контрольный обмер не выполнялся).
2. Шаг стоек 600 мм — по данным (под плитку и во влажной зоне). Размеры сечений профилей — «ПС 100», «УА 100» по данным и каталогу; толщины листов — ГОСТ 32614-2012.
3. Шаг стоек 600 мм принят по базовому правилу: в данных studStep не задан.
4. Проём Д-4 в каркасе 800 × 2100 мм принят по размеру полотна: короб скрытой двери (модель, размеры) не выбран — проём пересчитать по коробке до монтажа УА.
5. Перемычка над проёмом — направляющий профиль по верху проёма на всю его ширину; короткие стойки ПС над перемычкой на шаге каркаса: по практике узла Knauf, не по данным объекта.
6. Заполнение полости — минераловатная плита на всю глубину профиля (Rw системы С112 нормируют с заполнением); марка и плотность выбираются при закупке.
7. Длина стойки равна высоте перегородки: стойки режут на высоту между направляющими при монтаже, зазоры до плиты и пола в данных не заданы (edgeGaps).
8. Обшивку крепят к стойкам шурупами через слой, швы слоёв вразбежку; зазоры обшивки до плиты и пола, шаг дюбелей, марка заполнения — по ТУ системы и узлу изготовителя.

					Проект: Квартира 56 м²
	Лист	№ док.	Подпись	Дата	
Дизайнер	Кырлан А.С.			19.10.26	Схема каркаса перегородки П-2


Стадия	Лист	Листов
П	5	56

выпуск 19.10.2026 № 60226ce68e · стр. 5 из 56

Привязка выводов и крепление модулей

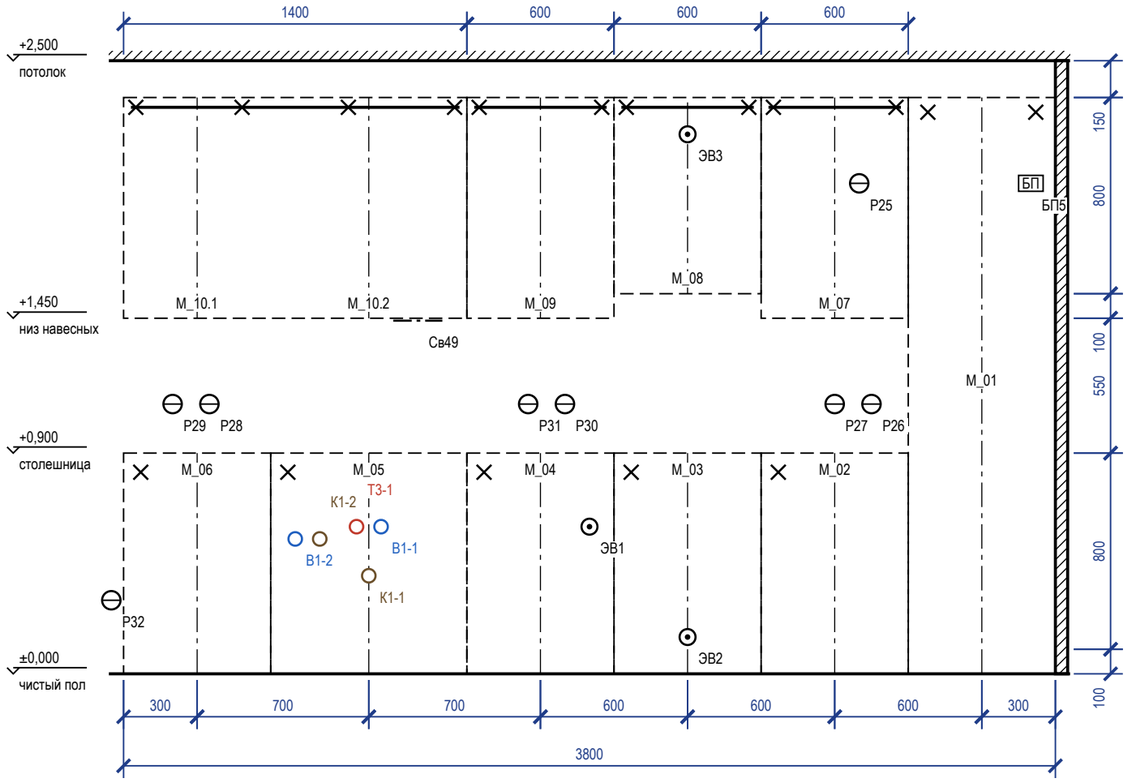

План столешницы

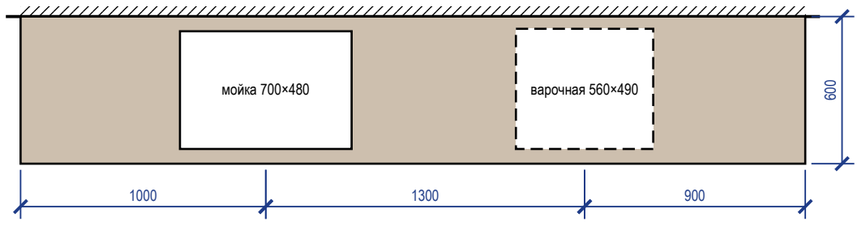

Примечания

1. Выводы — по проекту электрики и ВК; привязка по горизонтали — от оси модуля (плюс — вправо по виду), по высоте — от чистого пола до оси вывода.
2. Пенал — уголки к стене 2 шт. сверху; нижние модули — стяжками между собой и уголком к стене; ряд выставить по уровню опорами цоколя.
3. Розетки над столешницей — не ниже 150 мм над ней и не за корпусом техники; розетка за ПММ, духовым шкафом и холодильником — только в соседнем модуле или в зоне цоколя с доступом.
4. Столешница — вырезы по шаблонам выбранных моделей мойки и варочной панели; торцы у стены — герметик, пристеночный плинтус.

Привязка выводов к осям модулей

Код	Назначение	Модуль	От оси, мм	H, мм	Размещение
Р32	розетка — посудомоечная машина (на стене за торцом гарнитура, доступ сбоку)			300	вне гарнитура
Р29	розетка — фартук	М_06	−100	1100	над столешницей (фартук)
Р28	розетка ×2 — фартук	М_06	+50	1100	над столешницей (фартук)
В1-2	В1 — кран ПММ в шкафу мойки	М_05	−300	550	в модуле мойки
К1-2	К1 Ø40 — слив ПММ в шкафу мойки	М_05	−200	550	в модуле мойки
Т3-1	Т3 — межос. 100	М_05	−50	600	в модуле мойки
К1-1	К1 Ø50 — мойка	М_05	0	400	в модуле мойки
В1-1	В1 — межос. 100	М_05	+50	600	в модуле мойки
Св49	светодиодная лента — подсветка столешницы	М_05	+200	1440	в профиле по низу навесного модуля
Р31	розетка — фартук между мойкой и варочной	М_04	−50	1100	над столешницей (фартук)
Р30	розетка ×2 — фартук между мойкой и варочной	М_04	+100	1100	над столешницей (фартук)
ЭВ1	вывод кабеля — варочная панель (в соседнем модуле М_04, за ящиком)	М_04	+200	600	в соседнем модуле, за ящиком
ЭВ2	вывод кабеля — духовой шкаф	М_03	0	150	под духовым шкафом, доступ через ящик
ЭВ3	вывод кабеля — вытяжка	М_08	0	2200	в навесном модуле
Р27	розетка — фартук	М_02	0	1100	над столешницей (фартук)
Р25	розетка — холодильник (в навесном шкафу М_07, съёмная панель)	М_07	+100	2000	в навесном модуле
Р26	розетка ×2 — фартук	М_02	+150	1100	над столешницей (фартук)
БП5	блок питания — в пенале М6, верх, съёмная панель	М_01	+200	2000	над нишей холодильника, съёмная панель

Зазоры под отделку

Поверхность	Отделка	Зазор, мм	Учесть
фартук	керамогранит	10	от чернового основания до корпуса навесных и столешницы
стены	окраска	5	под штукатурку и шпаклёвку за пеналом
пол	инженерная доска		цоколь — после укладки пола, опоры ±20 мм

Условные обозначения


- навесной модуль (невидимый контур)
- ось модуля (от неё — привязка вывода)
- анкер / уголок крепления к стене
- розетка на стене
- вывод кабеля к технике
- В1 — вывод воды В1 / Т3, канализации К1

					Проект: Квартира 56 м²
	Лист	№ док.	Подпись	Дата	Кухня (пом. 1). Монтажная схема
Дизайнер	Кырлан А.С.			19.10.26	


Стадия	Лист	Листов
П	6	56

выпуск 19.10.2026 № 60226ce68e · стр. 6 из 56


Шкаф распашной М_19 (пом. 2)

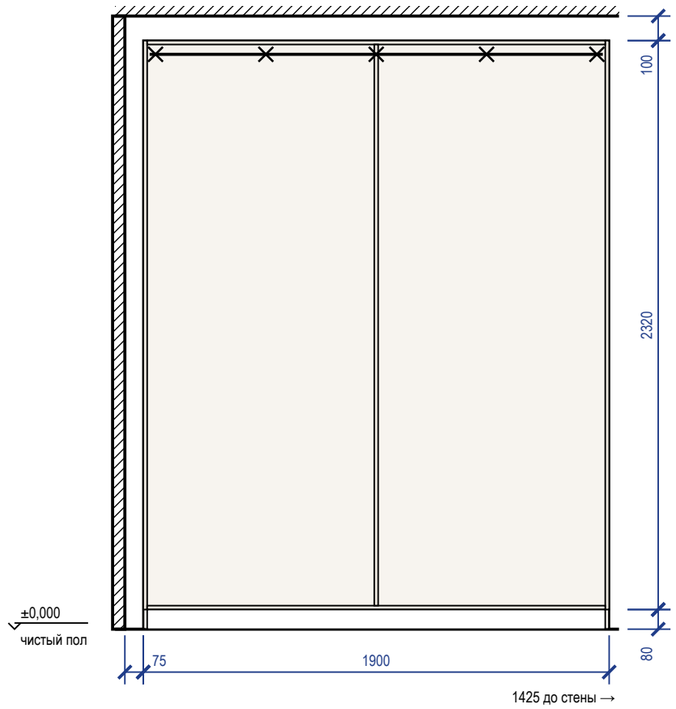


Шкаф распашной М_23 (пом. 3)

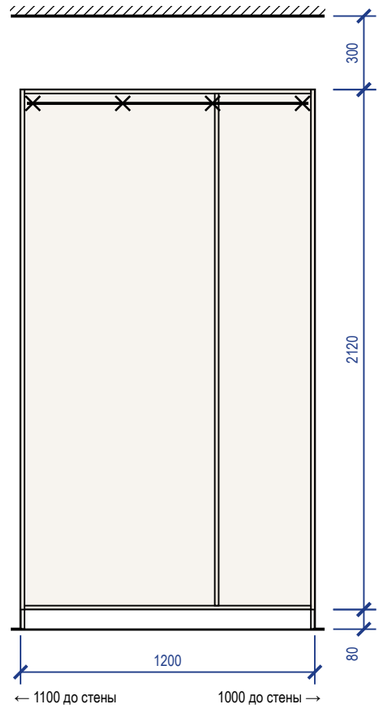

Шкаф-купе М_27 (пом. 5)

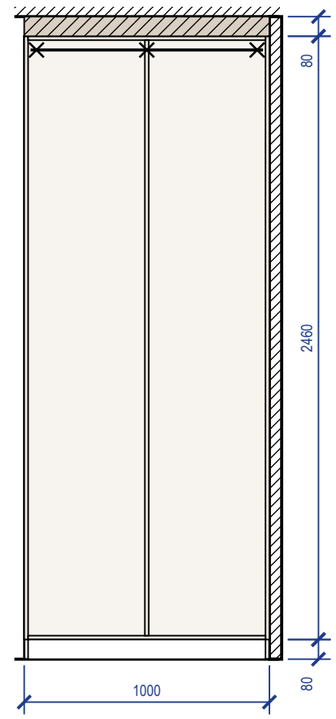

Система хранения М_29 (пом. 5)

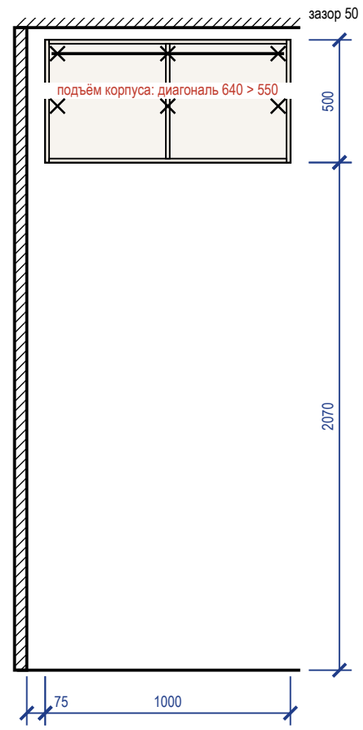

Крепление и зазоры под отделку

Марка	Помещение, стена	Основание	Отделка стены	Зазор, мм	Крепёж по планке	От опрокидывания
М_19	Спальня (2), стена В	по основанию — см. таблицу крепежа	окраска	5	анкер 5 шт., шаг 450	уголок к стене, 2 шт.
М_23	Детская (3), стена А	по основанию — см. таблицу крепежа	окраска	5	анкер 4 шт., шаг 367	уголок к стене, 2 шт.
М_27	Прихожая (5), стена В	по основанию — см. таблицу крепежа	окраска	5	анкер 3 шт., шаг 450	уголки 2 шт.
М_29	Прихожая (5), стена В	по основанию — см. таблицу крепежа	окраска	5	анкер 6 шт. (2 ряда)	true

Крепёж по основанию стены

Основание стены	Крепёж
бетон, ж/б	анкер-шуруп 7,5×72 или дюбель 8×60 с шурупом 5×70
кирпич полнотелый	дюбель 8×80 с шурупом 5×90
газобетон, пазогребень	дюбель для газобетона 10×100 или химический анкер
гипсокартон	закладная до обшивки (брус 40×80 или фанера 18 мм), саморез в закладную

Условные обозначения

- анкер / уголок крепления к стене
- корпус и полки ЛДСП (вид на стену)
- компенсатор — короб до потолка

Примечания


1. Установочные размеры — от чистого пола и чистых стен; перед установкой контрольный замер после отделки.
2. Порядок: корпус выставить по уровню опорами цоколя → закрепить к стене по задней планке → навесить двери и фасады, отрегулировать зазоры → подогнать и закрепить компенсатор.
3. Анкеры — с шагом не более 500 мм, не ближе 50 мм от края планки; на ГКЛ только в закладную, установленную до обшивки.
4. Скрытые коммуникации под анкеры проверить детектором; трассы электрики по плану розеток.

	Лист	№ док.	Подпись	Дата
Дизайнер	Кырлан А.С.			19.10.26

Проект: Квартира 56 м²

Шкафы. Монтажная схема	Стадия	Лист	Листов
	П	7	56

выпуск 19.10.2026 № 60226ce68e · стр. 7 из 56

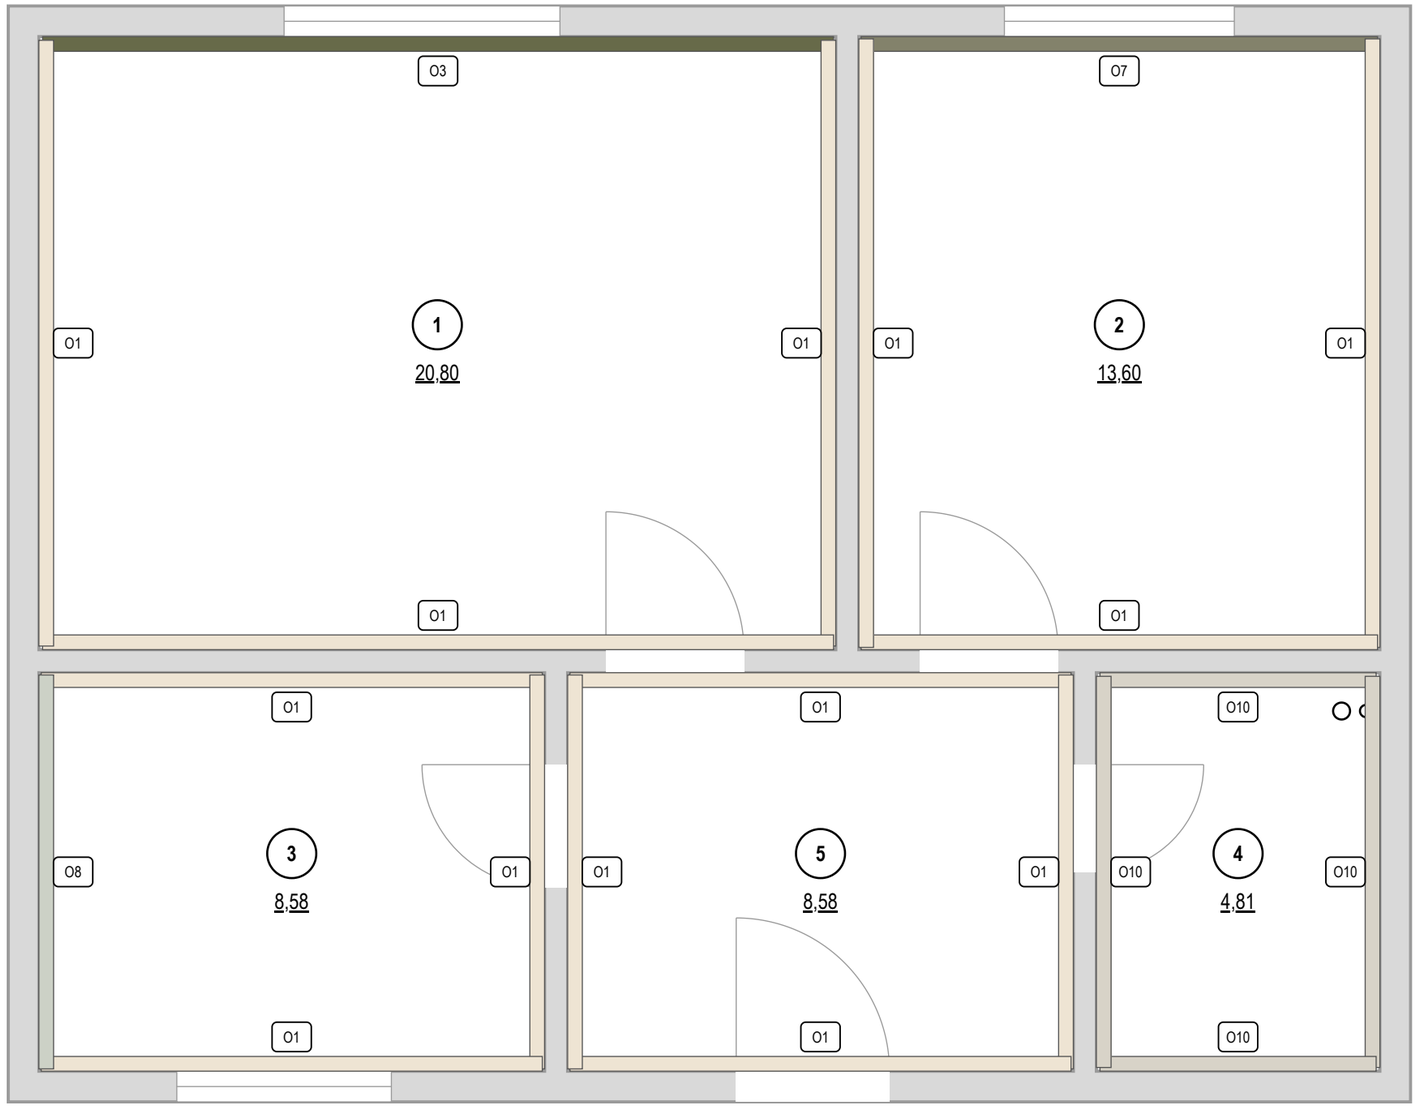
О3
1
20,80
О1
О1
О1
О7
2
13,60
О1
О1
О1

Колерная карта по помещениям

Помещение	Поверхность	Образец	Поз.	Система и код цвета	Производитель, линейка / материал, артикул	Блеск	Класс EN 13300	LRV	Площадь
1. Гостиная-кухня 20,8 м²	стены		**K1**	NCS S 0804-Y30R	Tikkurila · Euro Power 7, колеровка по NCS	матовая	1	78	29,3 м²
	акцент А		**K2**	Farrow & Ball No. 298	Farrow & Ball · Modern Emulsion	матовая	1	≈14	10,3 м²
	потолок		**K3**	Tikkurila F485	Tikkurila · Euro Power 7	глубокомат.	2	83	20,8 м²
	пол		**KM1**	по образцу	Coswick · Классическая				20,8 м²
	плинтус		**K4**	NCS S 0804-Y30R	МДФ · в цвет NCS			78	17,5 м
	фартук		**KM2**	по образцу	керамогранит · аналог по хар.				1,8 м²
2. Спальня 13,6 м²	стены		**K1**	NCS S 0804-Y30R	Tikkurila · Euro Power 7, колеровка по NCS	матовая	1	78	26,6 м²
	акцент А		**K5**	NCS S 5010-G70Y	Tikkurila · Euro Power 7, колеровка по NCS	матовая	1	22	6,3 м²
	потолок		**K3**	Tikkurila F485	Tikkurila · Euro Power 7	глубокомат.	2	83	13,6 м²
	пол		**KM1**	по образцу	Coswick · Классическая				13,6 м²
	плинтус		**K4**	NCS S 0804-Y30R	МДФ · в цвет NCS			78	13,9 м
3. Детская 8,58 м²	стены		**K1**	NCS S 0804-Y30R	Tikkurila · Euro Power 7, колеровка по NCS	матовая	1	78	19,3 м²
	акцент Г		**K6**	Tikkurila X447	Tikkurila · Euro Power 7	матовая	1	63	6,5 м²
	потолок		**K3**	Tikkurila F485	Tikkurila · Euro Power 7	глубокомат.	2	83	8,6 м²
	пол		**KM1**	по образцу	Coswick · Классическая				8,6 м²
	плинтус		**K7**	NCS S 0804-Y30R	Orac Decor · Contour (Luxxus)			78	11,0 м
4. Санузел 4,81 м²	стены		**K8**	Atlas Concorde A8UZ	Atlas Concorde · Marvel Travertine				19,9 м²
	потолок		**K9**	Tikkurila F485	Tikkurila · Euro Power 7	матовая	1	83	4,8 м²
	пол		**K8**	Atlas Concorde A8UZ	Atlas Concorde · Marvel Travertine				4,8 м²
5. Прихожая 8,58 м²	стены		**K1**	NCS S 0804-Y30R	Tikkurila · Euro Power 7, колеровка по NCS	матовая	1	78	21,9 м²
	потолок		**K3**	Tikkurila F485	Tikkurila · Euro Power 7	глубокомат.	2	83	8,6 м²
	пол		**K8**	Atlas Concorde A8UZ	Atlas Concorde · Marvel Travertine				8,6 м²
	плинтус		**K4**	NCS S 0804-Y30R	МДФ · в цвет NCS			78	7,5 м

Перечень выкрасов на согласование

№	Код	Бренд / веер	Пом. / стена	Подложка	Формат	Статус
1	S 0804-Y30R	NCS Tikkurila	1, 2, 3, 5	ГКЛ, загрунтованный под эту краску; МДФ, загрунтованный под эмаль	600×1000; 300×600	к выполнению
2	No. 298	Farrow & Ball	1 А	ГКЛ, загрунтованный под эту краску	600×1000	к выполнению
3	F485	Tikkurila	1, 2, 3, 4, 5	ГКЛ, загрунтованный под эту краску	600×1000	к выполнению
4	S 5010-G70Y	NCS Tikkurila	2 А	ГКЛ, загрунтованный под эту краску	600×1000	к выполнению
5	X447	Tikkurila	3 Г	ГКЛ, загрунтованный под эту краску	600×1000	к выполнению

Примечания

1. Цвет утверждается только по выкрасу на объекте: формат от А3 до 1000×1000 мм на загрунтованном ГКЛ, в 2 слоя (как на стене), не на белой шпаклёвке; смотреть днём и при свете проекта своего помещения, рядом с образцами пола и фасадов. Подпись на обороте: код, бренд и веер, дата.
2. Колеровка машинная в колеровочном центре бренда; каждый код — за один проход, одной партией на весь объём. Колеровщику передаётся только система и код утверждённого веера; плашки и HEX на листе — ориентир, печать не является эталоном цвета.
3. Класс мокрого истирания — EN 13300 (ISO 11998); блеск — по ГОСТ 31975 (ISO 2813), геометрия 60°. LRV — пересчёт координаты L каталога производителя (Y = ((L*+16)/116)³); «≈» — расчёт по HEX, справочно.
4. Площади поверхностей — тем же способом и с теми же цифрами, что в ведомости отделки (способ счёта — в общих указаниях); объём краски к заказу, фасовка и материалы КМ — в спецификации отделочных материалов.
5. Перечень выкрасов составлен по кодам колерной карты; к основному тону стен добавить на выкрас 2 соседних тона того же веера (светлее и темнее), статус отмечать в графе «Статус» при согласовании.

Схема квартиры: цвет стен и акценты (б/м)

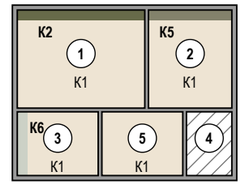


Схема палитры проекта


Стиль: Джапанди · схема: аналоговая

основной	основной	основной	второстепенный	второстепенный	второстепенный	акцентный	акцентный	акцентный
NCS S 0804-Y30R	**Tikkurila F485**	**Little Greene No. 105**	**Tikkurila X447**	**Tikkurila V484**	**NCS S 2005-Y30R**	**Farrow & Ball No. 298**	**NCS S 5010-G70Y**	**NCS S 7005-Y20R**
светлый «рисовая бумага» LRV 78 стены 1,2,3,5; плинтус 1,2,3,5	Damask LRV 83 потолок 1,2,3,4,5; текстиль/декор 1,2,3	Slaked Lime LRV 82 в отделке не применён	Sea Smoke LRV 63 акцент 3; текстиль/декор 1,2,3	Driftwood LRV 47 текстиль/декор 1,3	песочный грейж LRV 55 текстиль/декор 2	Bancha LRV ≈14 акцент 1; текстиль/декор 1	приглушённая олива LRV 22 акцент 2; текстиль/декор 2	тёмный орех LRV 9 в отделке не применён

План 60/30/10



Окраска, факт — по площади стен, акцентов, потолков

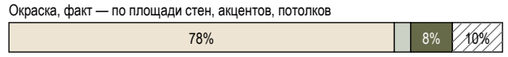

окрашено всего 196,5 м²; второстепенный тон несут мебель и текстиль

Текстиль и декор в цветах вне палитры проекта

NCS S 1002-Y50R тёплый светлый грейж — пом. 3 (Т10)

Условные обозначения

K1 NCS S 0804-Y30R · светлый «рисовая бумага» · Tikkurila Euro Power 7, колеровка по NCS · матовая · кл. 1

K2 Farrow & Ball No. 298 · Bancha · Modern Emulsion · матовая · кл. 1

K3 Tikkurila F485 · Damask · Euro Power 7 · глубокомат. · кл. 2

K4 NCS S 0804-Y30R · светлый «рисовая бумага» · МДФ

K5 NCS S 5010-G70Y · приглушённая олива · Tikkurila Euro Power 7, колеровка по NCS · матовая · кл. 1

K6 Tikkurila X447 · Sea Smoke · Euro Power 7 · матовая · кл. 1

дерево (доска, паркет, ламинат) — рисунок досок

керамогранит, плитка, камень — сетка швов по формату

HEX не задан — цвет только по коду и вееру

K7 NCS S 0804-Y30R · светлый «рисовая бумага» · Orac Decor Contour (Luxxus)

K8 Atlas Concorde A8UZ · Marvel Travertine · Marvel Travertine

K9 Tikkurila F485 · Damask · Euro Power 7 · матовая · кл. 1


KM1 инженерная доска · 1167-1101

KM2 аналог: керамогранит под травертин, матовый, 1200×600×9 мм

К — позиция окраски (код + продукт + блеск), КМ — позиция материала, тон КМ — по описанию артикула, эталон — образец материала; ≈ LRV — расчёт по HEX, справочно

					Проект: Квартира 56 м²
	Лист	№ док.	Подпись	Дата	
Дизайнер	Кырлан А.С.			19.10.26	Колерная карта

Стадия	Лист	Листов
П	9	56

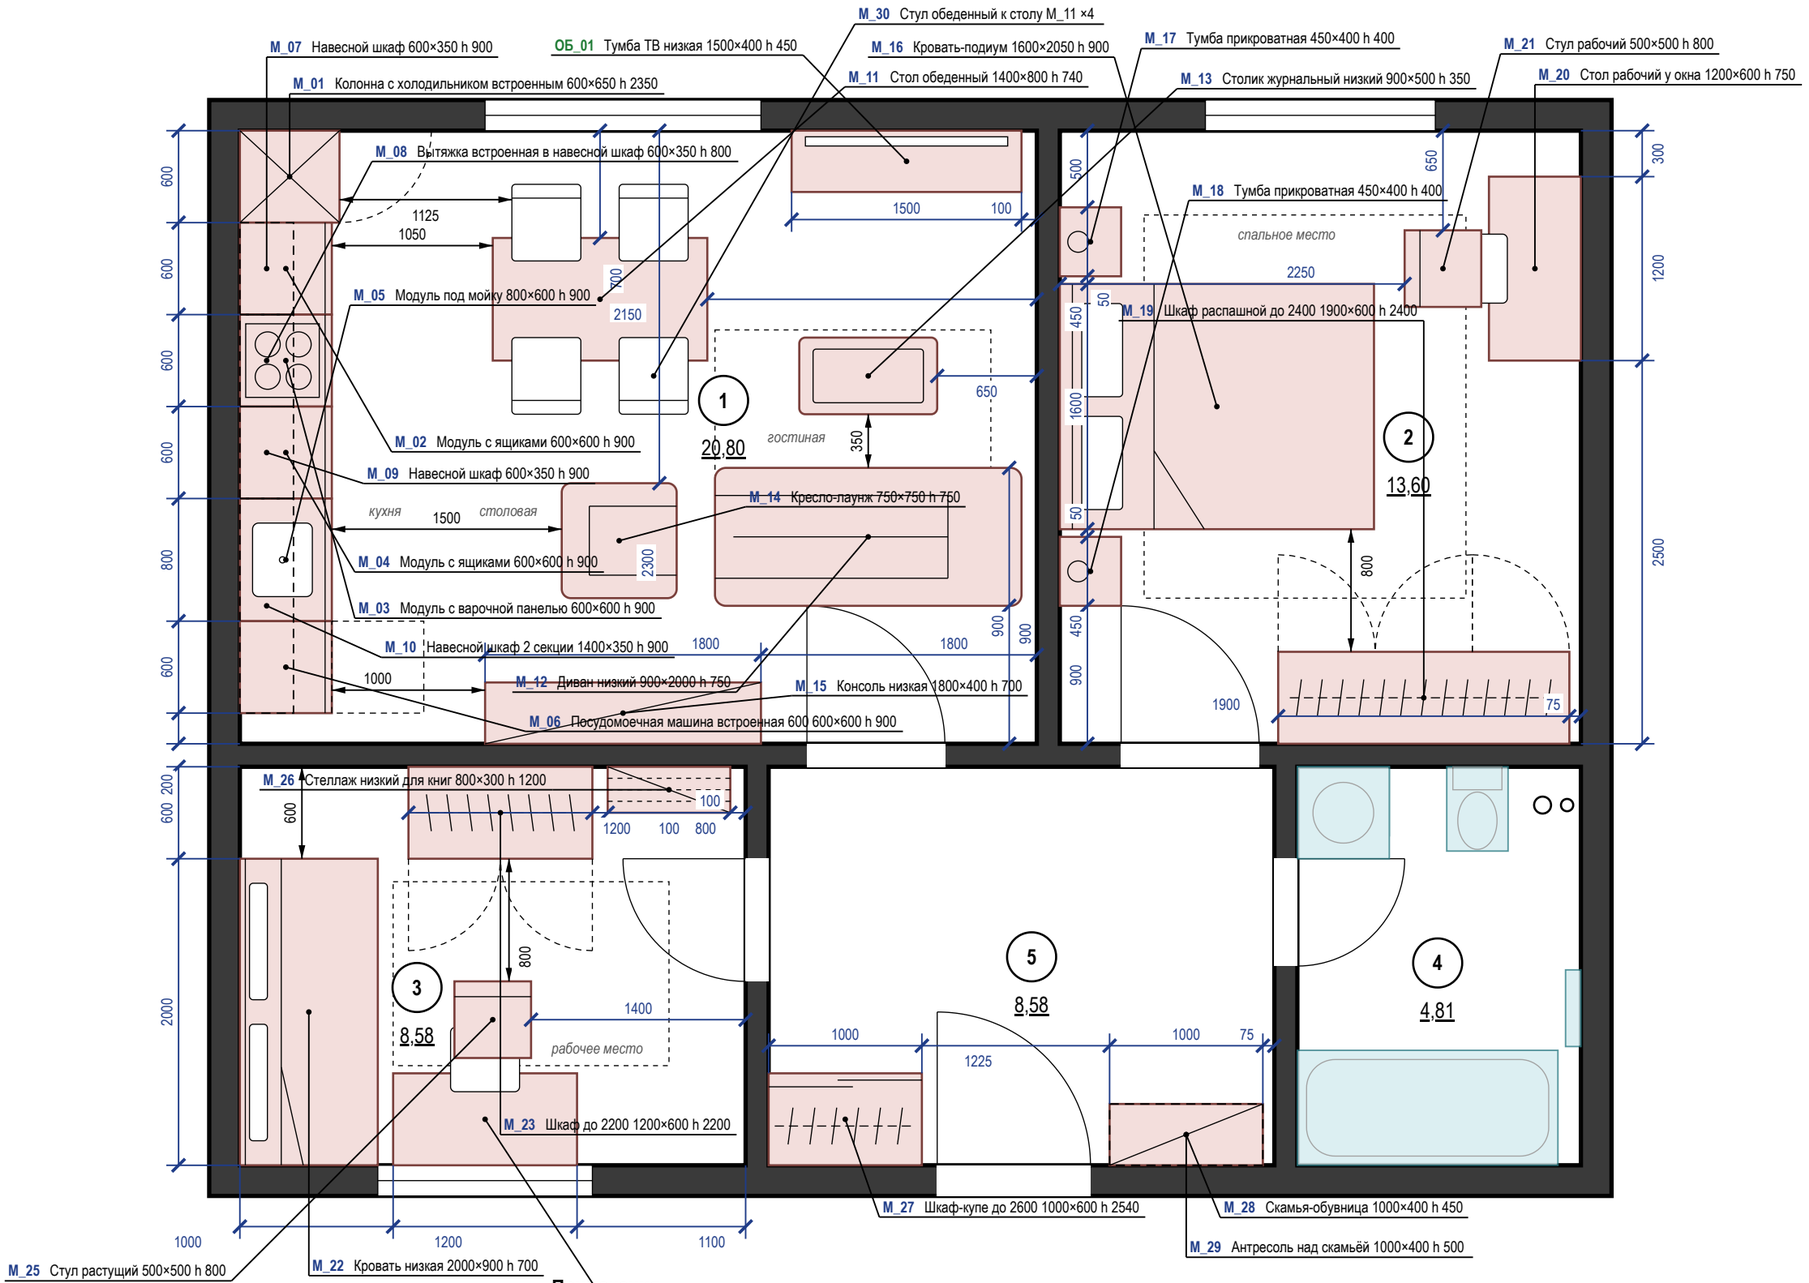

Примечания

1. Размеры — в мм от чистовых поверхностей стен; размеры мебели уточнить после отделочных работ; общие указания — лист 2.
2. Отступ от стены, на плане не образмерен: M_12 — 100 мм.
3. Стулья обеденной группы (M_30 — 4 шт.) показаны в рабочем положении, задвинутыми под столешницу на 150 мм.

Экспликация помещений

лист обмерного плана · на плане — номера в марках

Ведомость мебели и оборудования

Марка	Наименование	Ш×Г×В, мм	Пом.	Кол.
M_01	Колонна с холодильником встроенным	600×650×2350	1	1
M_02	Модуль с ящиками	600×600×900	1	1
M_03	Модуль с варочной панелью	600×600×900	1	1
M_04	Модуль с ящиками	600×600×900	1	1
M_05	Модуль под мойку	800×600×900	1	1
M_06	Посудомоечная машина встроенная 600	600×600×900	1	1
M_07	Навесной шкаф	600×350×900	1	1
M_08	Вытяжка встроенная в навесной шкаф	600×350×800	1	1
M_09	Навесной шкаф	600×350×900	1	1
M_10	Навесной шкаф 2 секции	1400×350×900	1	1
M_11	Стол обеденный 1400×800	1400×800×740	1	1
ОБ_01	Тумба ТВ низкая	1500×400×450	1	1
M_12	Диван низкий 2000×900	900×2000×750	1	1
M_13	Столик журнальный низкий	900×500×350	1	1
M_14	Кресло-лаунж	750×750×750	1	1
M_15	Консоль низкая 1800×400	1800×400×700	1	1
M_16	Кровать-подиум 1600×2000	1600×2050×900	2	1
M_17	Тумба прикроватная	450×400×400	2	1
M_18	Тумба прикроватная	450×400×400	2	1
M_19	Шкаф распашной 1900×600 до 2400	1900×600×2400	2	1
M_20	Стол рабочий у окна 1200×600	1200×600×750	2	1
M_21	Стул рабочий	500×500×800	2	1
M_22	Кровать 900×2000 низкая	2000×900×700	3	1
M_23	Шкаф 1200×600 до 2200	1200×600×2200	3	1
M_24	Стол письменный растущий 1200×600	1200×600×700	3	1
M_25	Стул растущий	500×500×800	3	1
M_26	Стеллаж низкий для книг	800×300×1200	3	1
M_27	Шкаф-купе 1000×600 до 2600	1000×600×2540	5	1
M_28	Скамья-обувница 1000×400	1000×400×450	5	1
M_29	Антресоль над скамьёй 1000×400	1000×400×500	5	1
M_30	Стул обеденный к столу M_11	450×500×820	1	4

Ш — вдоль стены (изголовья), Г — от стены (длина кровати)

Материалы, модели, допуск замены — лист 11

	Лист	№ док.	Подпись	Дата	Проект: Квартира 56 м²
Дизайнер	Кырлан А.С.			19.10.26	План размещения мебели и оборудования

Стадия	Лист	Листов
П	10	56

выпуск 19.10.2026 № 60226ce68e · стр. 10 из 56

Поз.	Наименование и техническая характеристика	Тип, марка, обозначение документа, опросного листа	Код продукции	Поставщик	Ед. измерения	Кол.	Масса 1 ед., кг	Примечание
	Мебель встроенная и корпусная (изготовление по чертежам мебельщика)							
M_01	Колонна с холодильником встроенным, фасад — дуб рифлёный; корпус ЛДСП, фасады — матовая эмаль в тон стен; Ш×Г×В 600×650×2350 мм			изготовление на заказ	шт.	1		пом. 1; крепление к стене
M_02	Модуль с ящиками; корпус ЛДСП, фасады — матовая эмаль в тон стен; Ш×Г×В 600×600×900 мм			изготовление на заказ	шт.	1		пом. 1
M_03	Модуль с варочной панелью и духовым шкафом; корпус ЛДСП, фасады — матовая эмаль в тон стен; Ш×Г×В 600×600×900 мм			изготовление на заказ	шт.	1		пом. 1
M_04	Модуль с ящиками; корпус ЛДСП, фасады — матовая эмаль в тон стен; Ш×Г×В 600×600×900 мм			изготовление на заказ	шт.	1		пом. 1
M_05	Модуль под мойку; корпус ЛДСП, фасады — матовая эмаль в тон стен; Ш×Г×В 800×600×900 мм			изготовление на заказ	шт.	1		пом. 1
M_06	Посудомоечная машина встроенная 600; корпус ЛДСП, фасады — матовая эмаль в тон стен; Ш×Г×В 600×600×900 мм			изготовление на заказ	шт.	1		пом. 1
M_07	Навесной шкаф, фасад — дуб рифлёный; корпус ЛДСП, фасады — матовая эмаль в тон стен; Ш×Г×В 600×350×900 мм			изготовление на заказ	шт.	1		пом. 1
M_08	Вытяжка встроенная в навесной шкаф, рециркуляция до обмера вентканала; корпус ЛДСП, фасады — матовая эмаль в тон стен; Ш×Г×В 600×350×800 мм			изготовление на заказ	шт.	1		пом. 1
M_09	Навесной шкаф; корпус ЛДСП, фасады — матовая эмаль в тон стен; Ш×Г×В 600×350×900 мм			изготовление на заказ	шт.	1		пом. 1
M_10	Навесной шкаф 2 секции, с сушкой; корпус ЛДСП, фасады — матовая эмаль в тон стен; Ш×Г×В 1400×350×900 мм			изготовление на заказ	шт.	1		пом. 1
M_19	Шкаф распашной 1900×600 до 2400, фасады — дуб рифлёный; корпус ЛДСП, фасады — матовая эмаль в цвет стен (NCS S 0804-Y30R); Ш×Г×В 1900×600×2400 мм			изготовление на заказ	шт.	1		пом. 2; крепление к стене
M_23	Шкаф 1200×600 до 2200, фасады — дуб и серо-зелёный; корпус ЛДСП, фасады — матовая эмаль в цвет стен (NCS S 0804-Y30R); Ш×Г×В 1200×600×2200 мм			изготовление на заказ	шт.	1		пом. 3; крепление к стене
M_27	Шкаф-купе 1000×600 до 2600, двери — дуб и зеркало; корпус ЛДСП, фасады — матовая эмаль в цвет стен (NCS S 0804-Y30R); Ш×Г×В 1000×600×2540 мм			изготовление на заказ	шт.	1		пом. 5
M_29	Антресоль над скамьёй 1000×400, фасад в цвет стены; каркас и полки — ЛДСП, декор «дуб натуральный»; Ш×Г×В 1000×400×500 мм			изготовление на заказ	шт.	1		пом. 5; крепление к стене
	Мебель покупная							
M_11	Стол обеденный 1400×800, массив дуба, низкие стулья Wishbone; шпон, дуб натуральный, матовое масло; Ш×Г×В 1400×800×740 мм			аналог по характеристикам	шт.	1		пом. 1; замена ≤ габарита
M_12	Диван низкий 2000×900, лён, сиденье 400; обивка — ткань, цвет Tikkurila X447; Ш×Г×В 900×2000×750 мм			аналог по характеристикам	шт.	1		пом. 1; замена ≤ габарита
M_13	Столик журнальный низкий, массив дуба; шпон, дуб натуральный, матовое масло; Ш×Г×В 900×500×350 мм			аналог по характеристикам	шт.	1		пом. 1; замена ≤ габарита
M_14	Кресло-лаунж, тёмный ясень и шерсть; обивка — ткань, цвет Tikkurila X447; Ш×Г×В 750×750×750 мм			аналог по характеристикам	шт.	1		пом. 1; замена ≤ габарита
M_15	Консоль низкая 1800×400, тёмный ясень, фасады рифлёные; шпон, дуб натуральный, матовое масло; Ш×Г×В 1800×400×700 мм			аналог по характеристикам	шт.	1		пом. 1; крепление к стене; замена ≤ габарита
M_30	Стул обеденный к столу M_11; обивка — ткань, цвет Tikkurila X447; каркас — дуб натуральный; Ш×Г×В 450×500×820 мм			аналог по характеристикам	шт.	4		пом. 1; замена ≤ габарита
ОБ_01	Тумба ТВ низкая, дуб, ТВ 55" шпон, дуб натуральный, матовое масло; Ш×Г×В 1500×400×450 мм			аналог по характеристикам	шт.	1		пом. 1; замена ≤ габарита
M_16	Кровать-подиум 1600×2000, дуб, изголовье 900; мягкое изголовье, обивка — ткань, цвет Tikkurila X447; Ш×Г×В 1600×2050×900 мм			аналог по характеристикам	шт.	1		пом. 2; замена ≤ габарита
M_17, M_18	Тумба прикроватная, дуб; шпон, дуб натуральный, матовое масло; Ш×Г×В 450×400×400 мм			аналог по характеристикам	шт.	2		пом. 2; замена ≤ габарита
M_20	Стол рабочий у окна 1200×600, дуб (работа из дома); шпон, дуб натуральный, матовое масло; Ш×Г×В 1200×600×750 мм			аналог по характеристикам	шт.	1		пом. 2; замена ≤ габарита
M_21	Стул рабочий, гнутая фанера; обивка — ткань, цвет Tikkurila X447; каркас — дуб натуральный; Ш×Г×В 500×500×800 мм			аналог по характеристикам	шт.	1		пом. 2; замена ≤ габарита
M_22	Кровать 900×2000 низкая, дуб, спинка-бортик 700 вдоль стены; мягкое изголовье, обивка — ткань, цвет Tikkurila X447; Ш×Г×В 2000×900×700 мм			аналог по характеристикам	шт.	1		пом. 3; замена ≤ габарита
M_24	Стол письменный растущий 1200×600; шпон, дуб натуральный, матовое масло; Ш×Г×В 1200×600×700 мм			аналог по характеристикам	шт.	1		пом. 3; замена ≤ габарита
M_25	Стул растущий; обивка — ткань, цвет Tikkurila X447; каркас — дуб натуральный; Ш×Г×В 500×500×800 мм			аналог по характеристикам	шт.	1		пом. 3; замена ≤ габарита
M_26	Стеллаж низкий для книг и игрушек 800×300; шпон, дуб натуральный, матовое масло; Ш×Г×В 800×300×1200 мм			аналог по характеристикам	шт.	1		пом. 3; крепление к стене; замена ≤ габарита
M_28	Скамья-обувница 1000×400, дуб; Ш×Г×В 1000×400×450 мм			аналог по характеристикам	шт.	1		пом. 5; замена ≤ габарита
	Техника встраиваемая и бытовая, светильники под розетки							
	Холодильник встраиваемый, в модуле M_01			аналог по характеристикам	шт.	1		пом. 1; по схеме изготовителя

Примечания

1. Позиции мебели совпадают с марками на плане расстановки; размеры Ш×Г×В — Ш вдоль стены, Г от стены.
2. Встроенная и корпусная мебель изготавливается по чертежам мебельщика после контрольного обмера; графы «Тип, марка» и «Код продукции» для неё не заполняются (ГОСТ 21.110-2013).
3. Покупные изделия — аналог по характеристикам: заменять только на изделия не больше указанного габарита и того же материала и цвета.
4. Материал и цвет, не указанные в данных изделия, приняты по концепции: тон дерева — по полу, обивка — по вторичному цвету палитры; образцы согласовать до заказа.
5. Масса 1 ед. для изделий до 25 кг не указывается. Техника — по монтажным схемам изготовителя; выводы — по листам ЭОМ и ВК.

					Проект: Квартира 56 м²
	Лист	№ док.	Подпись	Дата	Спецификация мебели и оборудования
Дизайнер	Кырлан А.С.			19.10.26	Стадия: П; Лист: 11; Листов: 56

Поз.	Наименование и техническая характеристика	Тип, марка, обозначение документа, опросного листа	Код продукции	Поставщик	Ед. измерения	Кол.	Масса 1 ед., кг	Примечание
	Варочная панель встраиваемая, электрическая, в модуле M_03			аналог по характеристикам	шт.	1		пом. 1; по схеме изготовителя
	Духовой шкаф встраиваемый, в модуле M_03			аналог по характеристикам	шт.	1		пом. 1; по схеме изготовителя
	Посудомоечная машина встраиваемая, в модуле M_06; ниша 600 мм			аналог по характеристикам	шт.	1		пом. 1; по схеме изготовителя
	Вытяжка встраиваемая, в модуле M_08			аналог по характеристикам	шт.	1		пом. 1; по схеме изготовителя
	Стиральная машина, место по листу ВК (ОБ_03); Ш×Г 600×600 мм			аналог по характеристикам	шт.	1		пом. 4; по схеме изготовителя
	Торшер, у поз. M_12; абажур — ткань или опаловое стекло; лампа 2700 K			аналог по характеристикам	шт.	1		пом. 1; розетка P21 (ЭОМ)
	Торшер, у поз. M_18; абажур — ткань или опаловое стекло; лампа 2700 K			аналог по характеристикам	шт.	1		пом. 2; розетка P5 (ЭОМ)
	Текстиль							
T13	Портьеры-волна (гостиная); лён 70 %, вискоза 30 %; цвет Tikkurila X447; карниз 2250 мм, высота 2610 мм, сборка 2			аналог по характеристикам	шт.	2		пом. 1
T14	Тюль (гостиная); полиэстер 100 %; цвет Tikkurila F485; карниз 2250 мм, высота 2610 мм, сборка 2,5			аналог по характеристикам	шт.	1		пом. 1
T16	Ковёр в зоне отдыха, джут с шерстью; шерсть 100 %; цвет Tikkurila V484; 1800×1600 мм			аналог по характеристикам	шт.	1		пом. 1; с подложкой
T17	Подушки на диван; букле (шерсть 60 %, полиэстер 40 %); цвет Tikkurila X447			аналог по характеристикам	шт.	3		пом. 1
T18	Подушки на диван, акцент; хлопковый бархат 100 %; цвет Farrow & Ball No. 298			аналог по характеристикам	шт.	2		пом. 1
T19	Плед на диван; альпака 50 %, шерсть 50 %; цвет Tikkurila V484			аналог по характеристикам	шт.	1		пом. 1
T1	Портьеры-волна; лён 100 %; цвет Tikkurila X447; карниз 2500 мм, высота 2610 мм, сборка 2			аналог по характеристикам	шт.	2		пом. 2
T2	Тюль; полиэстер 100 %; цвет Tikkurila F485; карниз 2500 мм, высота 2610 мм, сборка 2,5			аналог по характеристикам	шт.	1		пом. 2
T3	Ковёр под кроватью, шерсть; шерсть 80 %, хлопок 20 %; цвет NCS S 2005-Y30R; 2100×2500 мм			аналог по характеристикам	шт.	1		пом. 2; с подложкой
T4	Подушки декоративные на кровать; лён 100 %; цвет Tikkurila X447			аналог по характеристикам	шт.	3		пом. 2
T5	Подушки на кровать, акцент; хлопковый бархат 100 %; цвет NCS S 5010-G70Y			аналог по характеристикам	шт.	2		пом. 2
T6	Плед на кровать; шерсть мериноса 100 %; цвет NCS S 5010-G70Y			аналог по характеристикам	шт.	1		пом. 2
T7	Портьеры-волна; лён 100 %; цвет Tikkurila X447; карниз 1820 мм, высота 2610 мм, сборка 2			аналог по характеристикам	шт.	2		пом. 3
T8	Тюль; полиэстер 100 %; цвет Tikkurila F485; карниз 1820 мм, высота 2610 мм, сборка 2,5			аналог по характеристикам	шт.	1		пом. 3
T9	Ковёр игровой, шерсть; шерсть 100 %; цвет Tikkurila V484; 1800×1200 мм			аналог по характеристикам	шт.	1		пом. 3; с подложкой
T10	Подушки декоративные на кровать; букле (шерсть 60 %, полиэстер 40 %); цвет NCS S 1002-Y50R			аналог по характеристикам	шт.	3		пом. 3
T11	Подушки на кровать, акцент; хлопковый бархат 100 %; цвет Tikkurila X447			аналог по характеристикам	шт.	2		пом. 3
T12	Плед на кровать; шерсть мериноса 100 %; цвет Tikkurila X447			аналог по характеристикам	шт.	1		пом. 3
	Декор							
ДК6	Картина над консолью: горный ручей, тушь суми-э, рама — тёмный ясень; 1000×700 мм; низ на 950 мм от пола			аналог по характеристикам	шт.	1	6	пом. 1; крепление: анкер, 2 шт.
ДК7	Фикус каучуконосный в кашпо Ø450, глина; 450×450 мм			аналог по характеристикам	шт.	1		пом. 1
ДК8	Ваза керамическая с одной веткой на обеденном столе; 200×350 мм; на M_11			аналог по характеристикам	шт.	1		пом. 1
ДК1	Картина над кроватью: ветка сакуры, акварель, паспарту, рама — дуб; 1000×700 мм; низ на 1100 мм от пола			аналог по характеристикам	шт.	1	4	пом. 2; крепление к стене
ДК3	Картина над кроватью: кот на подоконнике, детская иллюстрация, рама — светлый дуб; 1200×600 мм; низ на 900 мм от пола			аналог по характеристикам	шт.	1	4	пом. 3; крепление к стене
ДК4	Зеркало в рост в тонкой чёрной раме; рама — чёрный матовый; 500×1500 мм; низ на 300 мм от пола			аналог по характеристикам	шт.	1	12	пом. 3; крепление: анкер для пустотелых оснований, 4 шт.
ДК2	Зеркало над умывальником, влагостойкое, с подсветкой; 600×800 мм; низ на 1200 мм от пола			аналог по характеристикам	шт.	1		пом. 4
ДК5	Зеркало над скамьёй, тонкая чёрная рама; рама — чёрный матовый; 600×1200 мм; низ на 700 мм от пола			аналог по характеристикам	шт.	1	18	пом. 5; крепление: анкер, 4 шт.

					Проект: Квартира 56 м²			
	Лист	№ док.	Подпись	Дата	Спецификация мебели и оборудования (продолжение)	Стадия	Лист	Листов
Дизайнер	Кырлан А.С.			19.10.26		П	12	56

выпуск 19.10.2026 № 60226ce68e · стр. 12 из 56

Ведомость изделий

Марка	Наименование	Пом.	Ш×Г×В, мм	Корпус	Фасад	Кромка, мм скр./вид.	Кол.
M_19	Шкаф распашной	2	1900×600×2400	ЛДСП 16	МДФ 18, эмаль матовая	0,4 / 2	1
M_23	Шкаф распашной	3	1200×600×2200	ЛДСП 16	МДФ 18, эмаль матовая	0,4 / 2	1
M_27	Шкаф-купе	5	1000×600×2540	ЛДСП 16	рифлёные панели МДФ в алюминиевом профиле	0,4 / 2	1
M_29	Система хранения	5	1000×400×500	ЛДСП 16	без фасадов; ящики — МДФ 18, эмаль матовая	0,4 / 2	1
M_06	Модуль нижний: ПММ	1	600×600×900	ЛДСП 16	МДФ 18, эмаль матовая	0,4 / 2	1
M_10	Модуль навесной: полки, сушка	1	1400×350×900	ЛДСП 16	МДФ 18, эмаль матовая	0,4 / 2	1
M_05	Модуль нижний: мойка	1	800×600×900	ЛДСП 16	МДФ 18, эмаль матовая	0,4 / 2	1
M_04	Модуль нижний: ящики	1	600×600×900	ЛДСП 16	МДФ 18, эмаль матовая	0,4 / 2	1
M_09	Модуль навесной: полки	1	600×350×900	ЛДСП 16	МДФ 18, эмаль матовая	0,4 / 2	1
M_03	Модуль нижний: духовой шкаф, варочная	1	600×600×900	ЛДСП 16	МДФ 18, эмаль матовая	0,4 / 2	1
M_08	Модуль навесной: полки	1	600×350×800	ЛДСП 16	МДФ 18, эмаль матовая	0,4 / 2	1
M_02	Модуль нижний: ящики	1	600×600×900	ЛДСП 16	МДФ 18, эмаль матовая	0,4 / 2	1
M_07	Модуль навесной: полки	1	600×350×900	ЛДСП 16	МДФ 18, эмаль матовая	0,4 / 2	1
M_01	Пенал: холодильник встр.	1	600×650×2350	ЛДСП 16	МДФ 18, эмаль матовая	0,4 / 2	1

Ведомость встраиваемой техники

Поз.	Прибор	Ниша, вырез, мм	Вентиляция	Питание	Схема
M_06	Посудомоечная машина встраиваемая, 60 см	ниша 600 × 862 (от пола до низа столешницы)	зазор в цоколе, по схеме	розетка в соседнем модуле	по модели
M_05	Мойка врезная / подстольная с сифоном	вырез по шаблону, ориентир 700 × 480		смеситель — выводы ВК	по модели
M_03	Духовой шкаф встраиваемый, 60 см	ниша 560 × 595, глубина ≥ 550	зазор за шкафом, вырез в задней стенке	вывод кабеля под шкафом	по модели
M_03	Варочная панель индукционная, 60 см	вырез в столешнице 560 × 490		вывод кабеля под модулем	по модели
M_01	Холодильник встраиваемый, ниша 1780	ниша 1780 × 560 × 550	решётка в цоколе, канал за корпусом, выход сверху	розетка над нишей или в соседнем модуле	по модели
M_03	Вытяжка настенная, 60 см	низ ≥ 650 над панелью	воздуховод к вентканалу, короб до потолка	вывод кабеля в коробе	по модели

Ведомость фурнитуры

№	Фурнитура	Тип, размер	Изделия	Кол.
1	Петля накладная 110° с доводчиком	чашка 35 мм	M_19, M_23, M_10, M_05, M_09, M_08, M_07, M_01	73
2	Полкодержатель с фиксацией	ø5 мм	M_19, M_23, M_27, M_29, M_10, M_09, M_08, M_07, M_01	112
3	Штанга овальная 30×15, L = 926	+ 2 держателя	M_19	1
4	Опора регулируемая с цоколем на клипсах	ход 20 мм	M_19, M_23, M_27	20
5	Анкер по основанию стены	по таблице крепежа	M_19, M_23, M_27, M_29, M_10, M_09, M_08, M_07	28
6	Уголок крепления к стене от опрокидывания	стальной	M_19, M_23, M_27, M_29, M_01	10
7	Штанга овальная 30×15, L = 776	+ 2 держателя	M_23	1
8	Система дверей купе: профиль, направляющие, ролики	на 2 двери	M_27	1
9	Ручка-профиль вертикальная	в цвет профиля	M_27	2
10	Штанга овальная 30×15, L = 476	+ 2 держателя	M_27	1
11	Полка для обуви выдвижная наклонная	ширина 476	M_27, M_29	6
12	Штанга выдвижная торцевая	L по глубине	M_29	1
13	Ручка-профиль	латунь матовая	M_06, M_10, M_05, M_04, M_09, M_03, M_08, M_02, M_07, M_01	23
14	Опора кухонная регулируемая 100–120 мм	+ клипса цоколя	M_06, M_05, M_04, M_03, M_02, M_01	26
15	Комплект навески фасада ПММ	из поставки машины	M_06	1
16	Сушка для посуды в шкаф	ширина 800	M_10	1
17	Навес регулируемый для навесного шкафа	пара на секцию	M_10, M_09, M_08, M_07	5
18	Шина монтажная	L = 1340	M_10	1
19	Направляющие полного выдвижения с доводчиком NL 500	пара	M_04, M_03, M_02	7
20	Шина монтажная	L = 540	M_09, M_08, M_07	3

Примечания


1. Модели техники выбирает заказчик до изготовления мебели; ниши, вырезы и вентиляция — по монтажной схеме выбранной модели (условие гарантии), её номер вносится в ведомость.
2. Количество фурнитуры — по чертежам изделий; запас крепежа 5 %. Аналоги — по характеристикам (доводчик, нагрузка, ход).
3. Цвет корпусов, фасадов и профилей — по колерной карте проекта.

					Проект: Квартира 56 м²
	Лист	№ док.	Подпись	Дата	Ведомости изделий, техники и фурнитуры
Дизайнер	Кырлан А.С.			19.10.26	


Стадия	Лист	Листов
П	13	56

выпуск 19.10.2026 № 60226ce68e · стр. 13 из 56

Фрагмент 1. Гостиная-кухня (пом. 1)

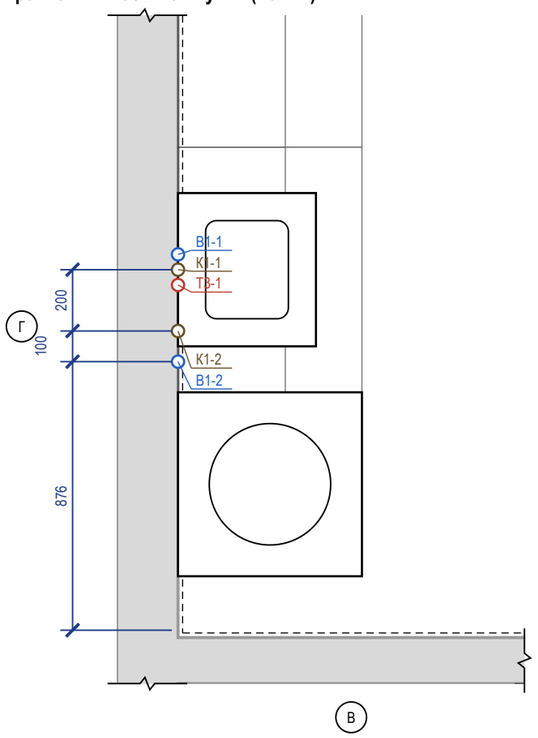

Фрагмент 2. Санузел (пом. 4)

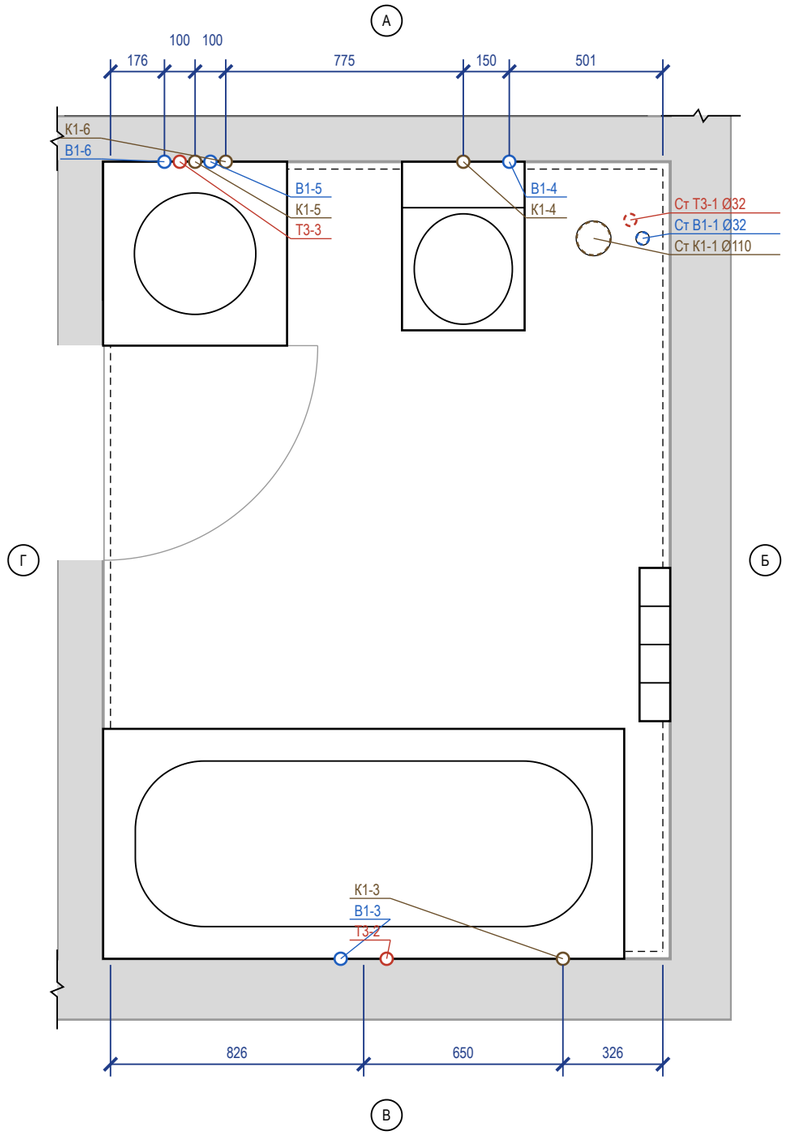

Ведомость привязок выводов

Код	Прибор	Ø	H, мм	Привязка от чист. стен, мм	Прим.
В1-1	С_01 мойка кухонная	½"	600	ст. Г: 1226 от В	межос. 100
Т3-1	С_01 мойка кухонная	½"	600	ст. Г: 1126 от В	межос. 100
К1-1	С_01 мойка кухонная	Ø50	400	ст. Г: 1176 от В	
В1-2	ОБ_02 посудомоечная машина	½"	550	ст. Г: 876 от В	кран ПММ в шкафу мойки
К1-2	ОБ_02 посудомоечная машина	Ø40	550	ст. Г: 976 от В	слив ПММ в шкафу мойки
В1-3	С_02 ванна	½"	800	ст. В: 751 от Г	межос. 150
Т3-2	С_02 ванна	½"	800	ст. В: 901 от Г	межос. 150
К1-3	С_02 ванна	Ø50	50	ст. В: 326 от Б	
В1-4	С_03 унитаз подвесной	½"	250	ст. А: 501 от Б	в раме инсталляции
К1-4	С_03 унитаз подвесной	Ø110	220	ст. А: 651 от Б	
В1-5	С_04 умывальник	½"	600	ст. А: 326 от Г	межос. 100
Т3-3	С_04 умывальник	½"	600	ст. А: 226 от Г	межос. 100
К1-5	С_04 умывальник	Ø50	500	ст. А: 276 от Г	
В1-6	ОБ_03 стиральная машина	½"	600	ст. А: 176 от Г	кран машины
К1-6	ОБ_03 стиральная машина	Ø50	600	ст. А: 376 от Г	

Условные обозначения


- вывод В1 (код — в ведомости привязок)
- вывод Т3 (код — в ведомости привязок)
- вывод К1 (код — в ведомости привязок)
- сантехприбор по расстановке (габарит модели)
- чистовая поверхность стены (от неё привязки)
- стояк «Ст К1-N / Ст В1-N» (ГОСТ 21.601), Ø мм
- стояк Т3 не на обмере — принят в шахте рядом со Ст В1, сверить
- линия обрыва (граница фрагмента)
- А — обозначение стены А–Г (как на развёртках)

Примечания


1. Привязки выводов даны от чистовых поверхностей стен (облицовка на сторону: гостиная-кухня — 24 мм (фартук: штукатурка 10 + клей 5 + плитка 9); санузел — 24 мм (штукатурка 10 + клей 5 + плитка 9)); эти же грани — на развёртках и в раскладке плитки. Высоты — от чистого пола помещения.
2. До черновой разводки сверить по паспорту выбранного прибора (смеситель, инсталляция, сифон).
3. Горячая вода (Т3) — слева от холодной (В1), если смотреть на прибор. Допуск установки выводов: ±5 мм в группе, ±20 мм у отдельно стоящих.
4. Расчёт систем водоснабжения и канализации и подбор оборудования выполняет проектная организация; лист задаёт места и высоты выводов.
5. Посудомоечная машина ОБ_02: кран и слив — отдельными выводами в шкафу мойки (не за машиной), до машины ≤ 1500 мм.
6. Ст К1-1, Ст В1-1, Ст Т3-1 на обмере не показаны: приняты рядом с Ст В1-1 (в МКД стоят группой); положение сверить на объекте до разметки.
7. Стояки в коробах/шахтах не замоноличивать; стояк К1 в коробе — звукоизоляция стояка в коробе без жёсткого контакта с трубой; к арматуре и ревизиям — люк не меньше 300×400.

					Проект: Квартира 56 м²
	Лист	№ док.	Подпись	Дата	План выводов сантехники
Дизайнер	Кырлан А.С.			19.10.26	Стадия: П; Лист: 14; Листов: 56


План квартиры (М 1:200)

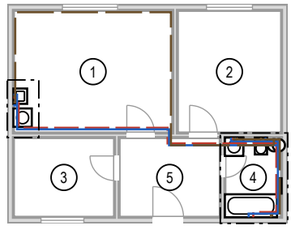

Фр. 1. Гостиная-кухня (М 1:20)

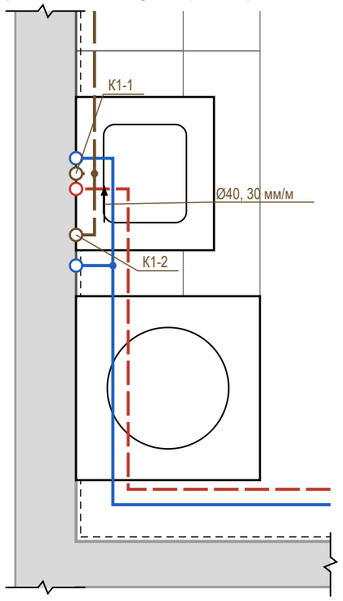

Фр. 2. Санузел (М 1:20)

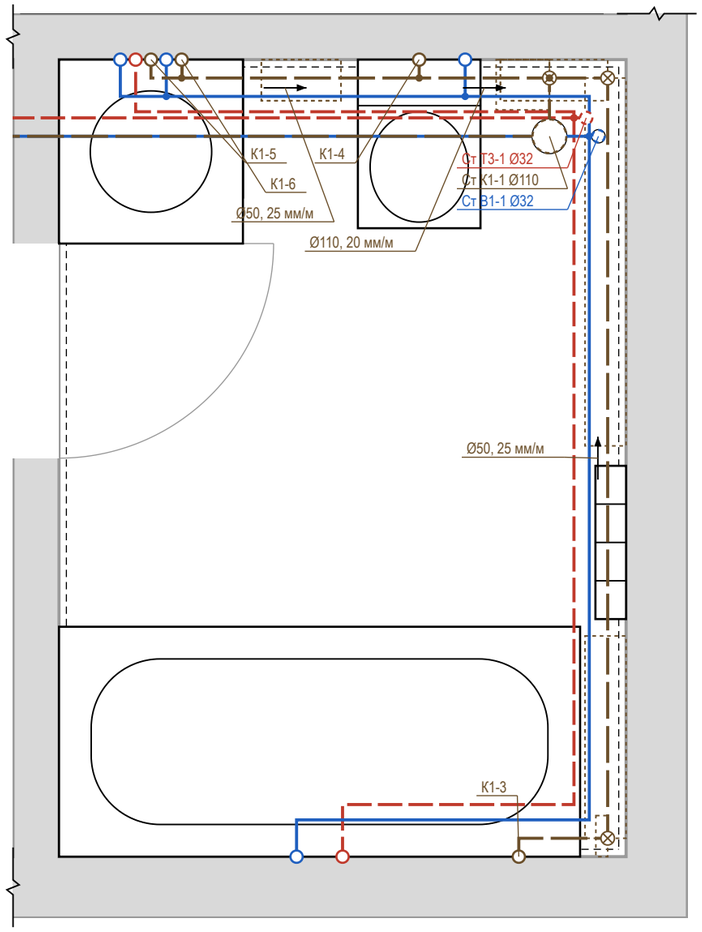

Условные обозначения

- В1 — водопровод хозяйственно-питьевой (ХВС), PP-R Ø20
- Т3 — горячее водоснабжение, подача (ГВС), PP-R Ø20
- К1 — канализация бытовая
- направление уклона К1 / пола: Ø, мм на 1 м
- ⊗ ревизия (прочистка) К1 — доступ сохранить
- • тройник (ответвление к прибору)
- ▭ короб К1 над чистым полом (ГКЛВ под плитку)
- ○ вывод В1 (код — в ведомости привязок)
- ○ вывод Т3 (код — в ведомости привязок)
- ○ вывод К1 (код — в ведомости привязок)
- ▭ сантехприбор по расстановке (габарит модели)
- ◯ стояк «Ст К1-N / Ст В1-N» (ГОСТ 21.601), Ø мм
- ◌ стояк Т3 не на обмере — принят в шахте рядом со Ст В1, сверить
- ⌇ линия обрыва (граница фрагмента)
- ▭ граница фрагмента на плане (Фр. N)

Профиль выпусков К1 (до врезки в стояк)

Выпуск	Прибор	Ø	L, м	i, мм/м	Δh, мм	Прокладка, мм
К1-4	С_03 унитаз подвесной	Ø110	0,68	20	14	короб 160×140
К1-1	С_01 мойка кухонная	Ø50	15,58	25	390	короб 470×110
К1-3	С_02 ванна	Ø50	3,21	25	80	короб 160×110
К1-5	С_04 умывальник	Ø50	1,55	25	39	короб 120×110
К1-6	ОБ_03 стиральная машина	Ø50	1,45	25	36	короб 120×110
К1-2	ОБ_02 посудомоечная машина	Ø40	15,78	30	473	короб 550×110

Короб h×b: h — от чистого пола, b — от чистовой стены. Стяжка 35 мм — лист полов.

Узел ввода В1, Т3 (схема, без масштаба)



⊗ Ст К1-1: ревизия на стояке — люк в коробе

Примечания

1. Трассы принципиальные, построены от стояков вдоль стен помещений; фактическое положение фиксируется исполнительной схемой с привязками (фото с рулеткой) до закрытия.
2. Уклон К1 не менее 1/d и не более 150 мм/м (СП 30.13330.2020, п. 19.1), приняты практические уклоны; поворот — двумя отводами 45°, ревизия после поворота, доступ сохранить. Стояк К1 в коробе — звукоизоляция стояка в коробе, без жёсткого контакта короба с трубой.
3. Решение по К1: стяжка 35 мм не укрывает трубы (нужно Ø + Δh + 45 мм) — выпуски идут над чистым полом вдоль стен; К1-4, К1-1, К1-3, К1-5, К1-6, К1-2 — в коробе ГКЛВ под плитку (размеры в профиле). Короба — на развёртках; отметку низа врезки в стояк замерить до черновых работ.
4. На каждом вводе В1 и Т3 — кран шаровой, фильтр, счётчик, обратный клапан; доступ через люк не меньше 300×400. Водопровод — в штробе стен или в коробах; трубы испытать давлением до закрытия (акт скрытых работ).
5. Расчёт систем, диаметры магистралей и подбор оборудования выполняет проектная организация; врезка и перенос стояков — по согласованию с управляющей организацией. Арматуру и привязки сверить по паспортам приборов.
6. Ст К1-1, Ст В1-1, Ст Т3-1 на обмере не показаны: приняты рядом с Ст В1-1; положение сверить на объекте до разводки.

					Проект: Квартира 56 м²
	Лист	№ док.	Подпись	Дата	Схема разводки водопровода и канализации
Дизайнер	Кырлан А.С.			19.10.26	

Стадия	Лист	Листов
П	15	56


Поз.	Наименование и техническая характеристика	Тип, марка, обозначение документа	Код продукции	Поставщик	Ед. изм.	Кол.	Масса 1 ед., кг	Примечание
	Санитарные приборы							
1	Ванна акриловая 1700×750 мм, с каркасом, экраном и отверстием слив-перелив	аналог		выбор заказчика	шт	1		С_02
2	Унитаз подвесной безободковый, с сиденьем микролифт, крепёж и звукоизолирующая прокладка	Laufen Pro 8.2096.6.000.000.1		выбор заказчика	шт	1		С_03
3	Инсталляция для подвесного унитаза: рама высотой 1120 мм, бачок, клавиша смыва (ось клавиши 1050 мм от чистого пола)	аналог		выбор заказчика	шт	1		С_03; короб ГКЛВ
4	Умывальник подвесной 600×450 мм, с отверстием под смеситель и переливом	аналог		выбор заказчика	шт	1		С_04
5	Мойка врезная, нержавеющая сталь, чёрная 500×450 мм, с переливом	аналог		с кухонной мебелью	шт	1		С_01
6	Полотенцесушитель электрический, IP44, с терморегулятором	аналог		выбор заказчика	шт	1		С_05
	Смесители, сифоны и арматура приборов							
7	Смеситель для ванны настенный однорычажный, межосевое 150 мм, с душевым набором (лейка, шланг, держатель)	аналог		выбор заказчика	шт	1		С_02
8	Смеситель для умывальника однорычажный, с донным клапаном	аналог		выбор заказчика	шт	1		С_04
9	Смеситель кухонный однорычажный, высокий излив	аналог		выбор заказчика	шт	1		С_01
10	Обвязка ванны слив-перелив Ø40/50 с сифоном	аналог		выбор заказчика	шт	1		С_02
11	Сифон для умывальника бутылочный Ø32/40–50, с гофрой к выпуску	аналог		выбор заказчика	шт	1		С_04
12	Сифон для мойки с отводом для ПММ Ø40/50	аналог		выбор заказчика	шт	1		С_01
13	Сифон для стиральной машины встраиваемый в стену Ø50, с обратным клапаном	аналог		выбор заказчика	шт	1		ОБ_03
14	Кран угловой ½"×½" с гибкой подводкой 40 см (умывальники, мойка)	аналог		выбор заказчика	шт	4		по 2 на прибор
15	Кран шаровой угловой ½"×¾" для подключения стиральной и посудомоечной машины	аналог		выбор заказчика	шт	2		ОБ_03, ОБ_02
	Трубопроводы							
16	Труба полипропиленовая PP-R PN20 Ø20×3,4 (В1)	ГОСТ 32415-2013		выбор заказчика	м	21,5	0,17	15,8 + 3,4 + 10 %
17	Труба PP-R, армированная стекловолокном, PN20 Ø20×2,8 (Т3)	ГОСТ 32415-2013		выбор заказчика	м	19	0,15	14,9 + 2,0 + 10 %
18	Труба канализационная ПП Ø40 (К1)	ГОСТ 32414-2013		выбор заказчика	м	1		0,3 + 0,6 + 10 %
19	Труба канализационная ПП Ø50 (К1)	ГОСТ 32414-2013		выбор заказчика	м	23,5		19,6 + 1,6 + 10 %
20	Труба канализационная ПП Ø110 (К1)	ГОСТ 32414-2013		выбор заказчика	м	1		0,7 + 0,2 + 10 %
	Фасонные части и выводы							
21	Отвод канализационный ПП 45° Ø40	ГОСТ 32414-2013		выбор заказчика	шт	2		2 шт. на поворот
22	Отвод канализационный ПП 45° Ø50	ГОСТ 32414-2013		выбор заказчика	шт	16		2 шт. на поворот
23	Отвод канализационный ПП 45° Ø110	ГОСТ 32414-2013		выбор заказчика	шт	4		2 шт. на поворот
24	Тройник канализационный ПП 45° (врезки ветвей)	ГОСТ 32414-2013		выбор заказчика	шт	5		
25	Ревизия канализационная ПП (после поворота трассы)	ГОСТ 32414-2013		выбор заказчика	шт	6		доступ сохранить
26	Фитинги PP-R Ø20: тройники, угольники 90° (ветви и повороты В1, Т3)	ГОСТ 32415-2013		выбор заказчика	шт	23		
27	Водорозетка PP-R Ø20×½" настенная, с креплением	ГОСТ 32415-2013		выбор заказчика	шт	9		коды — лист выводов
	Узлы ввода, люки, короба							
28	Кран шаровой латунный Ду15 PN16 (отключение ввода)	аналог		выбор заказчика	шт	2		Ст В1-1, Ст Т3-1
29	Фильтр сетчатый косой Ду15	аналог		выбор заказчика	шт	2		
30	Счётчик воды крыльчатый Ду15 (ХВ, ГВ), с поверкой	аналог		выбор заказчика	шт	2		пломба УК
31	Клапан обратный Ду15	аналог		выбор заказчика	шт	2		
32	Люк ревизионный нажимной под плитку 300×400 мм	аналог		выбор заказчика	шт	1		к стоякам и арматуре
33	Звукоизоляция стояка К1 в коробе: рулонный звукоизоляционный материал ≥ 10 мм, обмотка стояка на высоту этажа	аналог		выбор заказчика	м	2,7		Ст К1-1
34	Короб К1 над полом: профиль ПН/ПС, ГКЛВ 12,5 мм под плитку	аналог		выбор заказчика	м	16		сечение — лист разводки

Примечания

1. Форма 1 ГОСТ 21.110-2013, ширины граф изменены по п. 4.1. «Аналог» — аналог по характеристикам: модели внести до черновых работ, привязки выводов сверить по паспортам.
2. Бытовая техника не входит (показана арматура подключения), мойка — в комплекте кухни. Длины труб — трасса листа разводки + подъёмы + 10 %.
3. Стояк К1 в коробе — звукоизоляция стояка в коробе без жёсткого контакта короба с трубой.
4. Расчёт систем водоснабжения и канализации, диаметры магистралей и подбор оборудования выполняет проектная организация.

					Проект: Квартира 56 м²			
	Лист	№ док.	Подпись	Дата	Спецификация сантехнического оборудования	Стадия	Лист	Листов
Дизайнер	Кырлан А.С.			19.10.26		П	16	56

выпуск 19.10.2026 № 60226ce68e · стр. 16 из 56

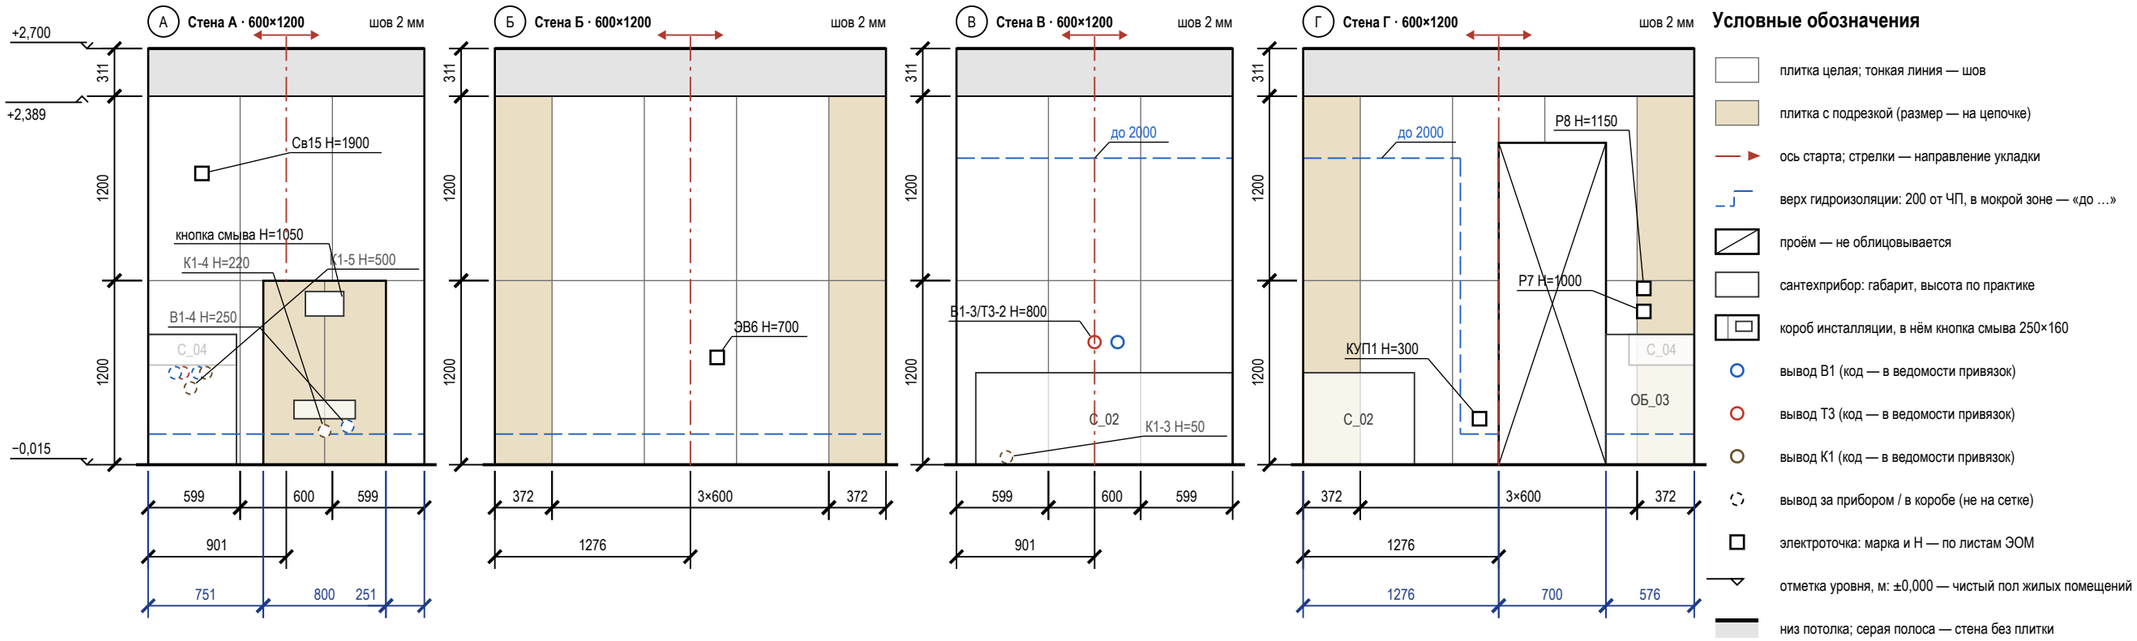

Условные обозначения

- плитка целая; тонкая линия — шов
- плитка с подрезкой (размер — на цепочке)
- ось старта; стрелки — направление укладки
- верх гидроизоляции: 200 от ЧП, в мокрой зоне — «до …»
- проём — не облицовывается
- сантехприбор: габарит, высота по практике
- короб инсталляции, в нём кнопка смыва 250×160
- вывод В1 (код — в ведомости привязок)
- вывод Т3 (код — в ведомости привязок)
- вывод К1 (код — в ведомости привязок)
- вывод за прибором / в коробе (не на сетке)
- электроточка: марка и Н — по листам ЭОМ
- отметка уровня, м: ±0,000 — чистый пол жилых помещений
- низ потолка; серая полоса — стена без плитки
- (А) обозначение стены А–Г (как на развёртках)

Подсчёт плитки по стенам и коробу

Поверхность	L × H, мм	S, м²	Целых	Подр.	С запасом	Подрезки: край / верх, мм
стена А	1802 × 2404	3,49	4	2	7	599 / 599; целый ряд
короб (ст. А)	800×1200×250	1,76	0	6	7	лицо 399 / 399; бок. 250
стена Б	2552 × 2404	6,25	6	4	11	372 / 372; целый ряд
стена В	1802 × 2404	4,45	6	0	7	599 / 599; целый ряд
стена Г	2552 × 2404	4,78	2	8	11	372 / 372; целый ряд
Итого		**20,73**	**18**	**20**	**43**	

Сдвиг точек под раскладку

Точка (ВК, ЭОМ)	Стена	Проект: от угла / Н	Под раскладку: от угла / Н	Сдвиг, мм
Св15	А	351 / 1900	299 / 1900	−52 в центр плитки
ЭВ6	Б	1451 / 700	1577 / 700	+126 на шов
В1-3/Т3-2	В	976 / 800	901 / 800	−75 в центр плитки
Р7, Р8	Г	2223 / 1000, 1150	2179 / 1000, 1150	−44 на шов
КУП1	Г	1151 / 300	1276 / 300	+125 в центр плитки

Примечания

1. Вид изнутри, стены по часовой стрелке А → Г. Высоты — от чистого пола (−0,015), отметки — от ±0,000. Раскладка от чистовых размеров (штукатурка 10 + клей 5 + плитка 9 мм), подрезки чистые; старт — от оси стены, ряды от пола целыми.
2. Верх плитки +2,389, потолок +2,700, зазор 311 мм: потолок ГКЛ опустить до +2,392 (шов 3 мм, герметик) — согласовать с монтажником ГКЛ; иначе профиль-окантовка, полосу окрасить в цвет потолка. Подрезной ряд 306 мм не делать.
3. Точки из таблицы сдвигов переносятся до черновой разводки: смеситель — по оси пары В1 + Т3; вывод на оси прибора — вместе с прибором, иначе старт раскладки — на ось прибора.
4. За приборами и в коробе (В1-4, К1-4, Т3-3/В1-5, К1-5, В1-6, К1-6, К1-3) — штриховым кольцом.
5. Гидроизоляция: 200 мм от ЧП по периметру; над ванной — до 2000 и 300 мм за борт (СП 29.13330.2011, п. 7.2 — на высоту замачивания); углы — лентой; акт скрытых работ, пролив.
6. Короб 800×1200×250: лицо 399 / 399 мм от оси кнопки смыва, боковины, полка; углы — запил 45° или профиль; за коробом плитку не кладут.

					Проект: Квартира 56 м²
	Лист	№ док.	Подпись	Дата	Раскладка плитки. Санузел. Развёртки стен
Дизайнер	Кырлан А.С.			19.10.26	Стадия: П; Лист: 17; Листов: 56


выпуск 19.10.2026 № 60226ce68e · стр. 17 из 56

Ведомость заполнения проёмов

Марка	Наименование, обозначение	Проём ш×в, мм	Кол.	Откр.	Отделка полотна	Фурнитура	Прим.
Д-1	Блок дверной входной, ГОСТ 31173-2016	1000×2100	1	Л	в комплекте блока	в комплекте блока (замки, глазок)	пом. 5; наружу
Д-2	Дверь скрытого монтажа, ТУ изготовителя	900×2100	1	П	окраска S 0804-Y30R с двух сторон	скрытые петли 3D, магнитный замок	
Д-3	Дверь скрытого монтажа, ТУ изготовителя	900×2100	1	П	окраска S 0804-Y30R с двух сторон	скрытые петли 3D, магнитный замок	
Д-4	Дверь скрытого монтажа, ТУ изготовителя	800×2100	1	Л	окраска S 0804-Y30R с двух сторон	скрытые петли 3D, магнитный замок	
Д-5	Дверь скрытого монтажа, ТУ изготовителя	700×2100	1	П	в тон облицовки — пом. 4, S 0804-Y30R — пом. 5	скрытые петли 3D, магнитный замок, фиксатор WC	пом. 4; порог 15
ОК-1	Блок оконный, ГОСТ 23166-2021	1800×1500	1				пом. 1; низ 850
ОК-2	Блок оконный, ГОСТ 23166-2021	1500×1450	1				пом. 2; низ 900
ОК-3	Блок оконный, ГОСТ 23166-2021	1400×1450	1				пом. 3; низ 900


Примечания

1. Размеры проёмов и привязки — в миллиметрах от чистых граней стен до отделки; привязка — от угла того помещения, со стороны которого стоит размер. Размер в ведомости — ширина × высота проёма от чистого пола 0,000. Откос от угла помещения до проёма с коробкой — не менее 50 мм.
2. Марки в кружках — типы заполнения проёмов (ГОСТ 21.501-2018, п. 5.3.2); одна марка — один типоразмер; количество сверено с планом.
3. Открывание: Л — петли слева, П — справа, если смотреть со стороны, куда открывается полотно (на себя).
4. Скрытые двери (Д-2…Д-5): проём замерить в чистоте; блок заказать до штукатурки (≈ 30 дн.), короб ставить до штукатурки; полотно навесить после чистовой отделки, красить в цвет стен. Порядок практика монтажа, изготовитель подтверждает.
5. Д-2, Д-3, Д-5 — существующие проёмы, до техзаключения не расширять.
6. Экспликация помещений — лист 3; в марках помещений — номер и площадь, м².

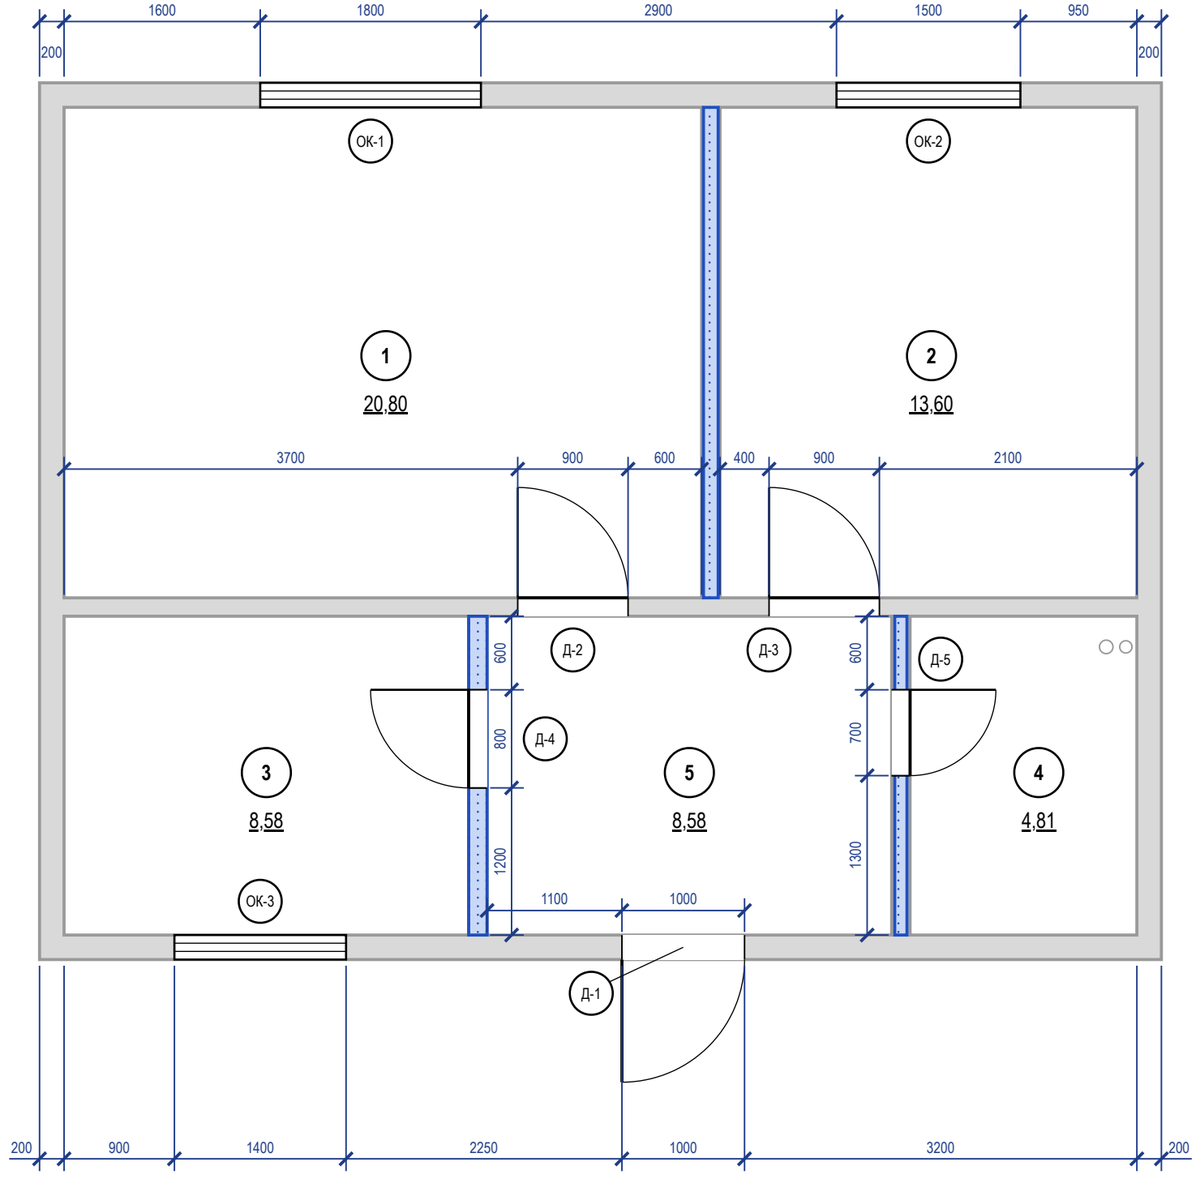

					Проект: Квартира 56 м²			
	Лист	№ док.	Подпись	Дата	План размещения дверей	Стадия	Лист	Листов
Дизайнер	Кырлан А.С.			19.10.26		П	18	56

выпуск 19.10.2026 № 60226ce68e · стр. 18 из 56

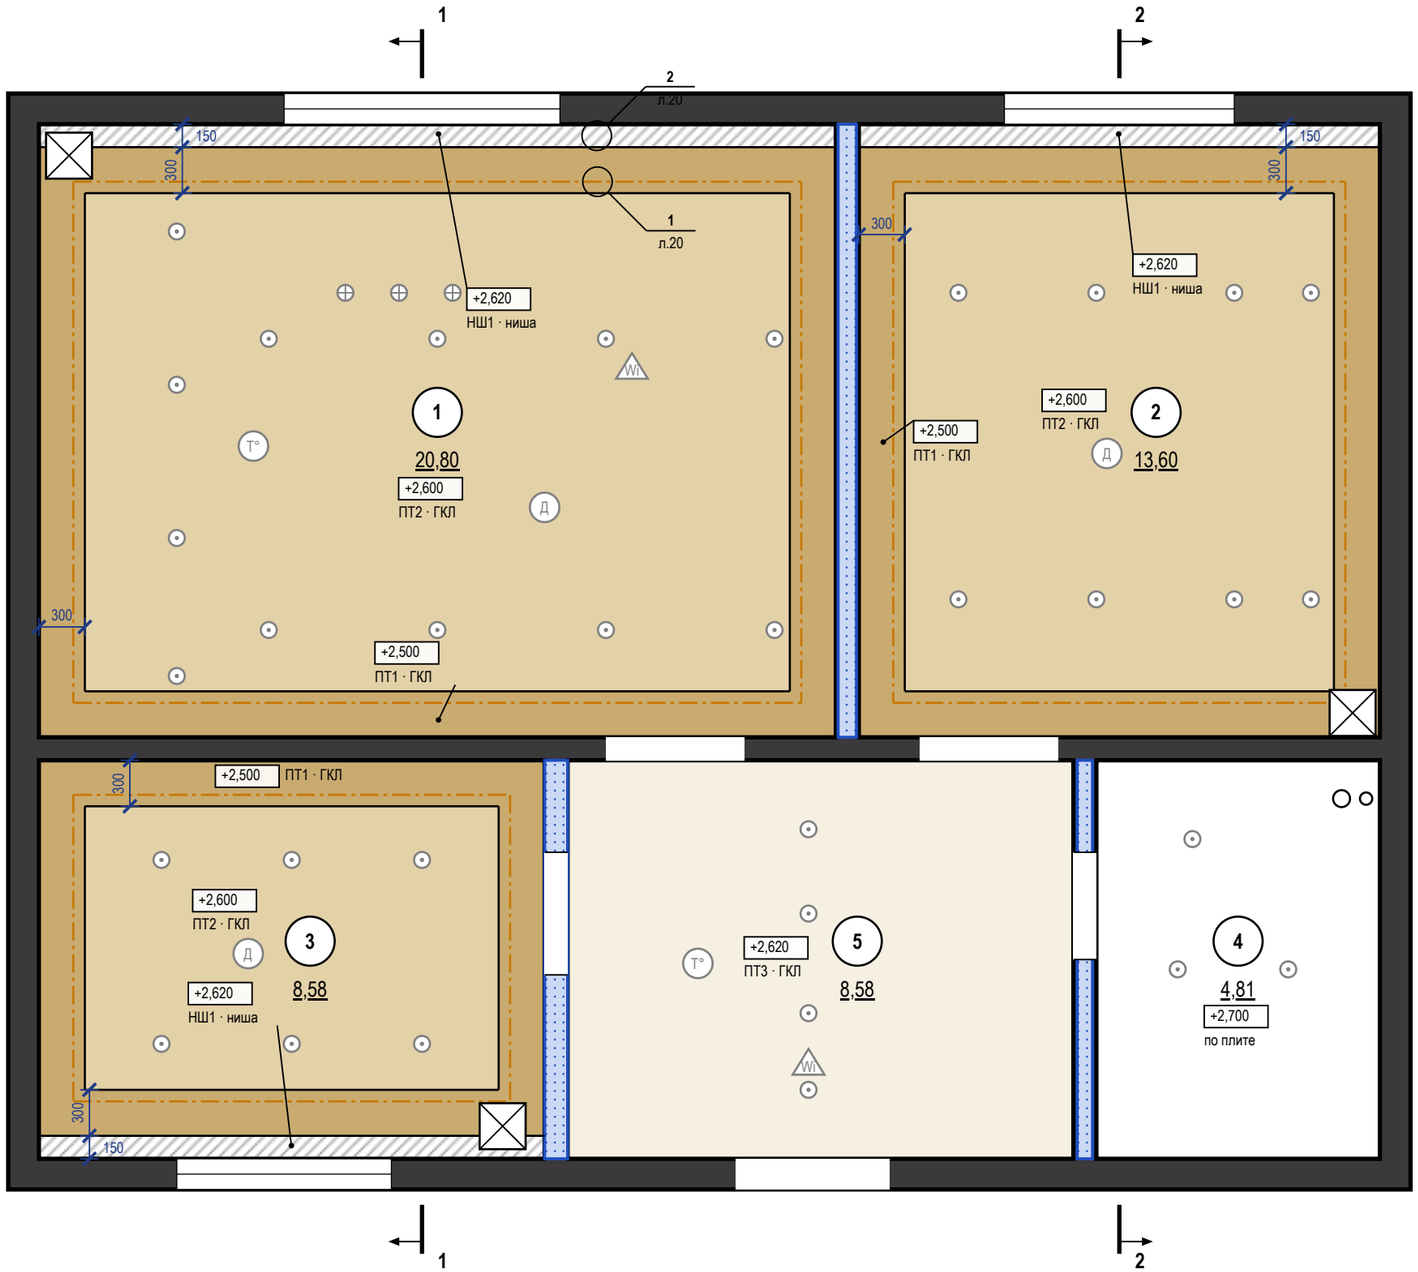

Ведомость потолков

Пом.	Марка	Конструкция	Низ	S, м²	Q
1	ПТ1	ГКЛ П113, короб LED	+2,500	5,07	Q3
1	ПТ2	ГКЛ П113	+2,600	14,95	Q3
1	НШ1	ниша под шторы 150×120	+2,620	0,78	
2	ПТ1	ГКЛ П113, короб LED	+2,500	3,99	Q3
2	ПТ2	ГКЛ П113	+2,600	9,10	Q3
2	НШ1	ниша под шторы 150×120	+2,620	0,51	
3	ПТ1	ГКЛ П113, короб LED	+2,500	3,09	Q3
3	ПТ2	ГКЛ П113	+2,600	5,00	Q3
3	НШ1	ниша под шторы 150×120	+2,620	0,49	
4		по плите, окраска	+2,700	4,81	
5	ПТ3	ГКЛ П113	+2,620	8,58	Q3
		Итого		**56,37**	

Ведомость вырезов и закладных в потолке

Марка	Устройство	Кол.	Пом.
	Светильник встраиваемый (марки — план освещения)	33	1, 2, 3, 4, 5
	Светильник подвесной (марки — план освещения)	3	1
ИП4, ИП1, ИП2	Извещатель дымовой	3	1, 2, 3
ИП5, ИП3	Извещатель тепловой	2	1, 5
АР2, АР1	Точка доступа Wi-Fi, PoE	2	1, 5
	Люк ревизии 300×300	3	1, 2, 3

Примечания

1. За отметку ±0,000 принят уровень чистого пола сухих помещений (готовое покрытие), а не существующего пола; пол пом. 4 — −0,015; верх плиты перекрытия −0,064 — расчётный по пирогу пола, не замерен; существующий пол снимается до плиты, его отметка не замерена. Отметки в прямоугольниках — низ потолка; низ плиты перекрытия +2,700. Марка потолка — одна конструкция и отметка на весь альбом.
2. Потолки ГКЛ — каркасная система П113: подвесы через 1000, несущие профили через 500, основные через 1200 мм; листы — поперёк несущих профилей.
3. Нижний уровень — пояс-короб по периметру шириной 300 мм (карниз подсветки + 150 мм полки), верхний — поле внутри пояса.
4. LED-лента в алюминиевом профиле посередине карниза короба шириной 300 мм (узел 1, лист 20); длина по плану: пом. 1 — 16,3 м (в плане освещения 16,3); пом. 2 — 12,7 м (в плане освещения 12,7); пом. 3 — 9,7 м (в плане освещения 9,7).
5. Ниши под шторы 150×120 мм — на всю длину стены с окном; карниз — на закладной до обшивки (узел 2, лист 20).
6. Примыкание к стенам: теневой шов 15 мм, техзазор 3 мм — пом. 1, 2, 3, по стенам, выровненным штукатуркой (узел 1); пом. 5 — разделительная лента.
7. Светильники и потолочные устройства — подложка с планов освещения, слаботочных систем и вентиляции (положение — по ним); вырезы и закладные — по ведомости на листе, до обшивки; отверстия не совмещать с профилями, глубина корпуса светильника до 70 мм.
8. Разрезы 1–1, 2–2 и узлы — на листе 20; высоты мебели и дверных блоков сверены с низом потолка в разрезах.
9. Шпаклевание ГКЛ и условия приёмки — Q3: рассеянный дневной свет, осмотр с 2 м; боковой свет не оценивается.
10. Люки ревизии 300×300 мм — по центру блоков питания LED (БП4, БП1, БП2; координаты — план освещения).
11. Пом. 4 — потолок по плите без подвесной системы; отделка — по ведомости отделки.


					Проект: Квартира 56 м²
	Лист	№ док.	Подпись	Дата	План потолков
Дизайнер	Кырлан А.С.			19.10.26	

Стадия	Лист	Листов
П	19	56

выпуск 19.10.2026 № 60226ce68e · стр. 19 из 56


Разрез 1–1 (М 1:40)

Пом. 1 Гостиная-кухня; линия разреза — план потолков, лист 19

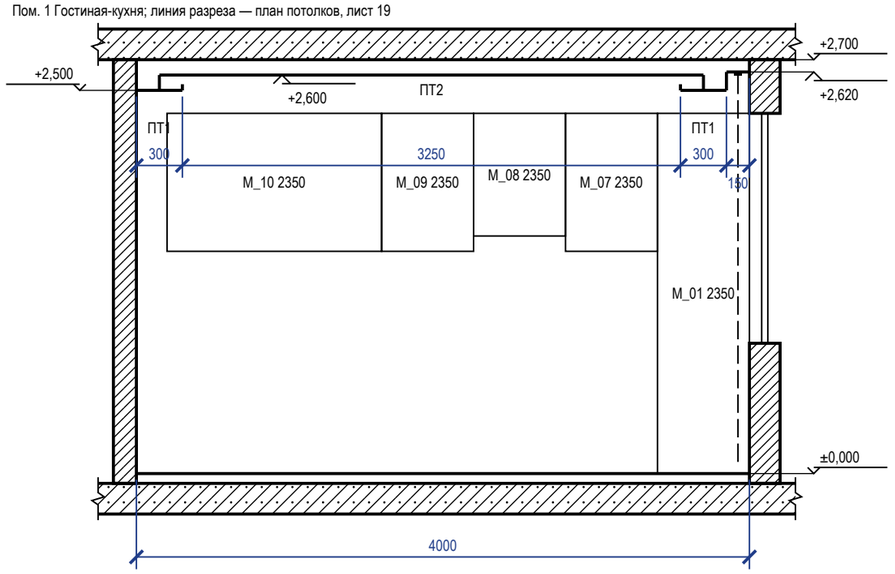


Разрез 2–2 (М 1:40)

Пом. 2 Спальня; линия разреза — план потолков, лист 19

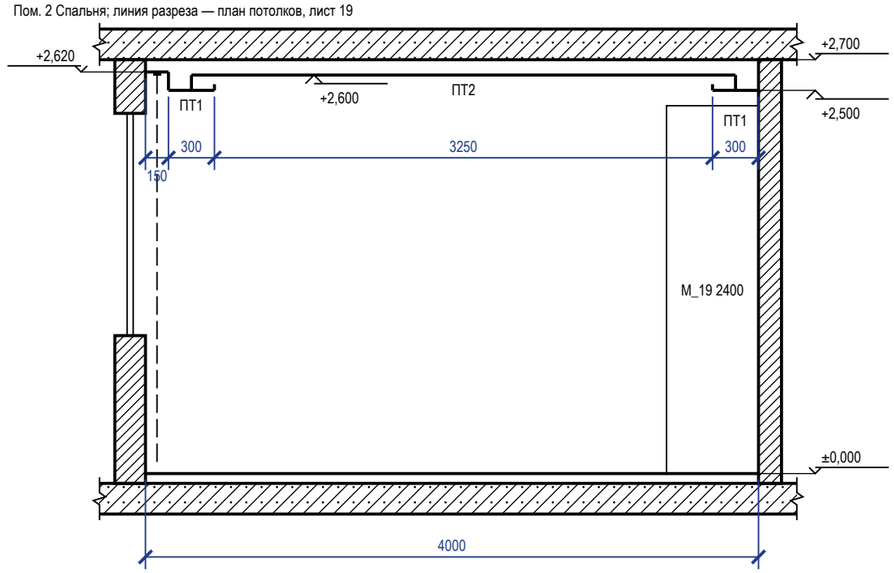

1 Короб с LED-подсветкой, теневой шов (М 1:10)


Пом. 1, 2, 3; карниз 150×100, щель под свет 60 мм

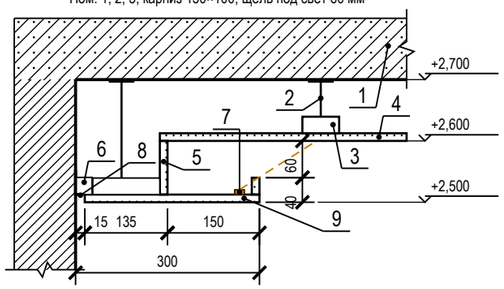

1 — плита перекрытия
2 — подвес прямой, шаг 1000 мм
3 — ПП 60×27: несущие через 500, основные через 1200 мм
4 — ГКЛ 12,5 по П113 — верхний уровень
5 — задняя стенка и бортик карниза — ГКЛ 12,5
6 — ПН 28×27 по периметру, к стене через 500 мм
7 — LED-лента в алюминиевом профиле
8 — теневой профиль: шов 15 мм, зазор 3 мм
9 — низ короба — ГКЛ 12,5 по ПП 60×27

2 Ниша под шторы (М 1:10)

Пом. 1, 2, 3; без подсветки; закладные под карниз — до обшивки

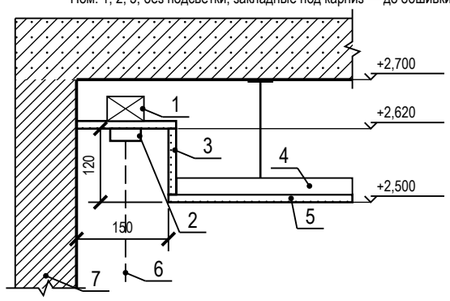

1 — закладная под карниз — брус 40×50
2 — карниз (шина), высота с верхом портьеры 100 мм
3 — стенка и потолок ниши — ГКЛ 12,5
4 — ПП 60×27 — каркас короба
5 — низ короба нижнего уровня — ГКЛ 12,5
6 — портьера
7 — стена с окном

Условные обозначения


- плита перекрытия в сечении
- стена в сечении
- потолок ГКЛ в сечении; под линией — марка потолка (план потолков)
- мебель и дверные проёмы за секущей плоскостью; число — марка и верх от чистого пола, мм
- портьера в нише под шторы

Примечания

1. Разрезы — по линиям 1–1, 2–2 на плане потолков (лист 19). Отметки — от ±0,000 чистого пола, м; размеры — мм.
2. Высоты мебели и дверных блоков за секущей плоскостью сверены с низом потолка над ними: верх ниже низа короба и поля.
3. ГКЛ 12,5 мм по каркасу П113; перепад уровней и бортик карниза — ГКЛ по ПП 60×27 (узел 1). Ниша под шторы — на всю длину стены с окном, карниз на закладной до обшивки (узел 2).
4. Толщины плит перекрытия и пирога пола показаны условно.

					Проект: Квартира 56 м²	
	Лист	№ док.	Подпись	Дата	Разрезы и узлы потолков	Стадия / Лист / Листов
Дизайнер	Кырлан А.С.			19.10.26		П / 20 / 56

выпуск 19.10.2026 № 60226ce68e · стр. 20 из 56

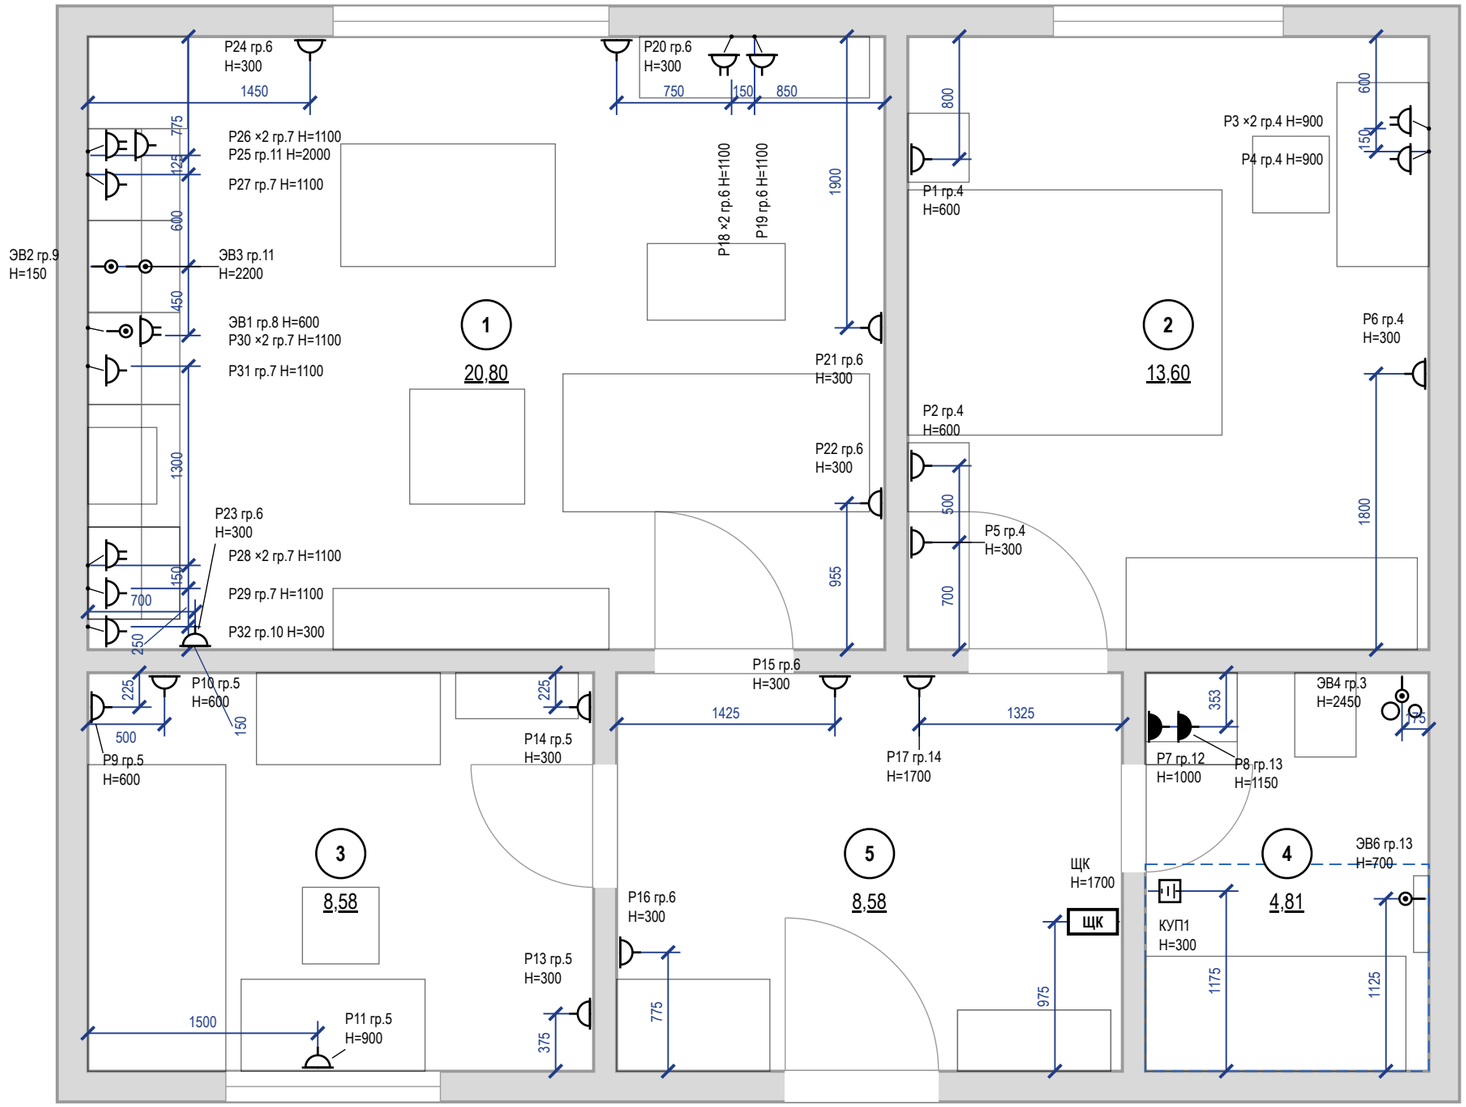

Условные обозначения


- розетка с заземляющим контактом; у знака — марка, ×N постов в рамке, гр. — группа щита, Н — высота оси, мм
- то же, рамка на 2 поста (число черточек — число постов)
- розетка влагозащищённая IP44
- вывод кабеля для подключения прибора (без розетки), марка ЭВ
- КУП — коробка уравнивания потенциалов (ДСУП), проводник к шине РЕ щита
- ЩК — щит квартирный
- знак разведён для читаемости: точка на стене — у выноски, привязка — до неё
- граница зоны 2 ванной (600 мм от ванны/поддона)
- мебель и сантехприборы — подложка
- стояк: К1 — канализация, В1 — ХВС, Т3 — ГВС
- 1 — номер помещения, площадь м²

Примечания

1. За отметку 0,000 принят уровень чистого пола. Высоты Н — от чистого пола до оси изделия; привязки — от чистовой грани стены до оси механизма (у рамки на несколько постов — до оси рамки).
2. Высота установки, не указанная на плане: розетки — 300 мм от чистого пола; выводы кабеля — по паспорту прибора.
3. Розетки в санузле — только вне зон 0–2 (ПУЭ 7.1.48, ГОСТ Р 50571.7.701-2024), IP44, через УЗО 30 мА.
4. Розеточные и мокрые линии — через УЗО или дифавтомат с током утечки не более 30 мА (ПУЭ 7.1.79); в санузле выполнить ДСУП (ПУЭ 7.1.87–7.1.88).
5. Кабель — медный, исполнение нг(А)-LS (ГОСТ 31565-2012); скрытая прокладка только горизонтально и вертикально, фактические трассы зафиксировать исполнительной схемой до закрытия отделкой.
6. Расчёт нагрузок, токов КЗ, селективности и сечений — по проекту ЭОМ организации с допуском СРО; лист задаёт состав, расположение и группы.
7. Выводы кухонной техники — после утверждения проекта кухни (ориентировочно); привязки выводов даны от осей модулей гарнитура и пересматриваются вместе с проектом кухни.
8. Электрический тёплый пол проектом не предусмотрен; при решении заказчика устроить — отдельный лист «План тёплых полов»: контуры с отступом 100 мм от стен и мебели без ножек, датчик в гофре, терморегулятор, своя группа щита через УЗО 30 мА.
9. Ведомости электроточек, изделий, светильников и расшифровка клавиш — лист «Ведомость электроточек и изделий».

					Проект: Квартира 56 м²			
	Лист	№ док.	Подпись	Дата	План розеток и электровыводов	Стадия	Лист	Листов
Дизайнер	Кырлан А.С.			19.10.26		П	21	56

выпуск 19.10.2026 № 60226ce68e · стр. 21 из 56

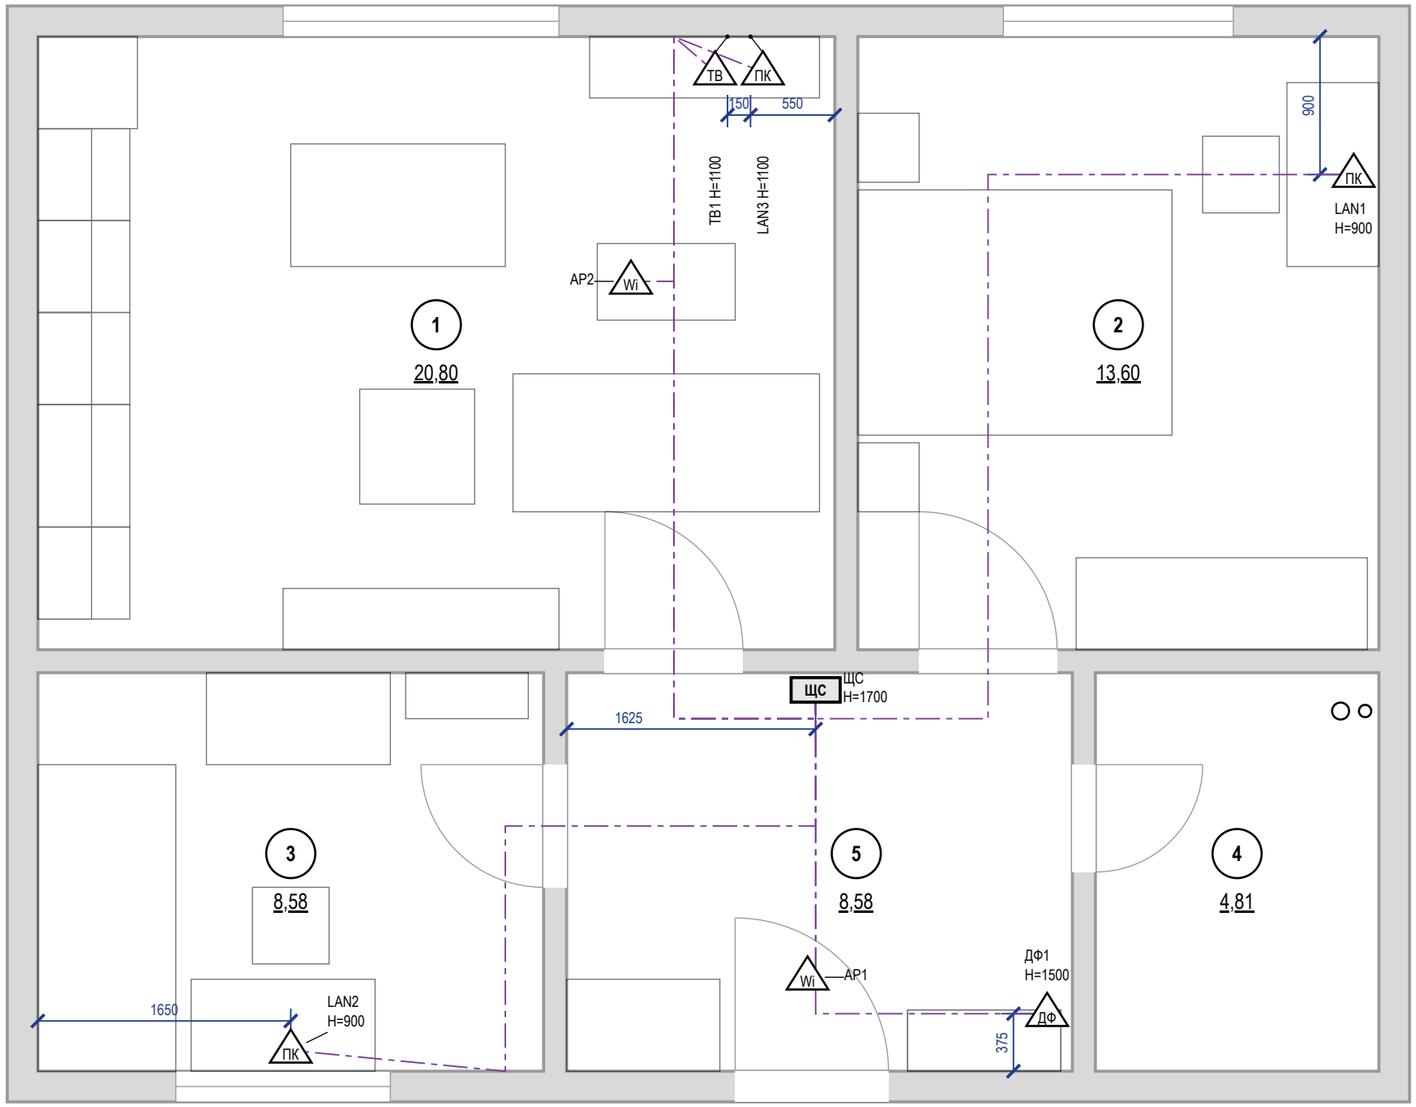


Примечания

1. За отметку 0,000 принят уровень чистого пола. Высоты H — от чистого пола до оси изделия; привязки — от чистовой грани стены до оси механизма (у рамки на несколько постов — до оси рамки).
2. Высота установки, не указанная на плане: розетки LAN и ТВ — 300 мм от чистого пола.
3. Слаботочные кабели — отдельно от силовых: в своей трубе или лотке, при параллельной прокладке не ближе 100 мм к силовым, пересечения под прямым углом; каждую точку — отдельным кабелем от ЩС без скруток.
4. Трассы на листе — принципиальные; фактические зафиксировать исполнительной схемой до закрытия отделкой. Силовые линии, УЗО 30 мА, ДСУП, кабель нг(A)-LS — по листам розеток и щита.
5. Проект силовой части и расчёт токов КЗ — по проекту ЭОМ; слаботочная часть согласуется с провайдером и управляющей компанией (домофон, коллективное ТВ).

					Проект: Квартира 56 м²
	Лист	№ док.	Подпись	Дата	
Дизайнер	Кырлан А.С.			19.10.26	План слаботочных сетей

Стадия	Лист	Листов
П	22	56

выпуск 19.10.2026 № 60226ce68e · стр. 22 из 56

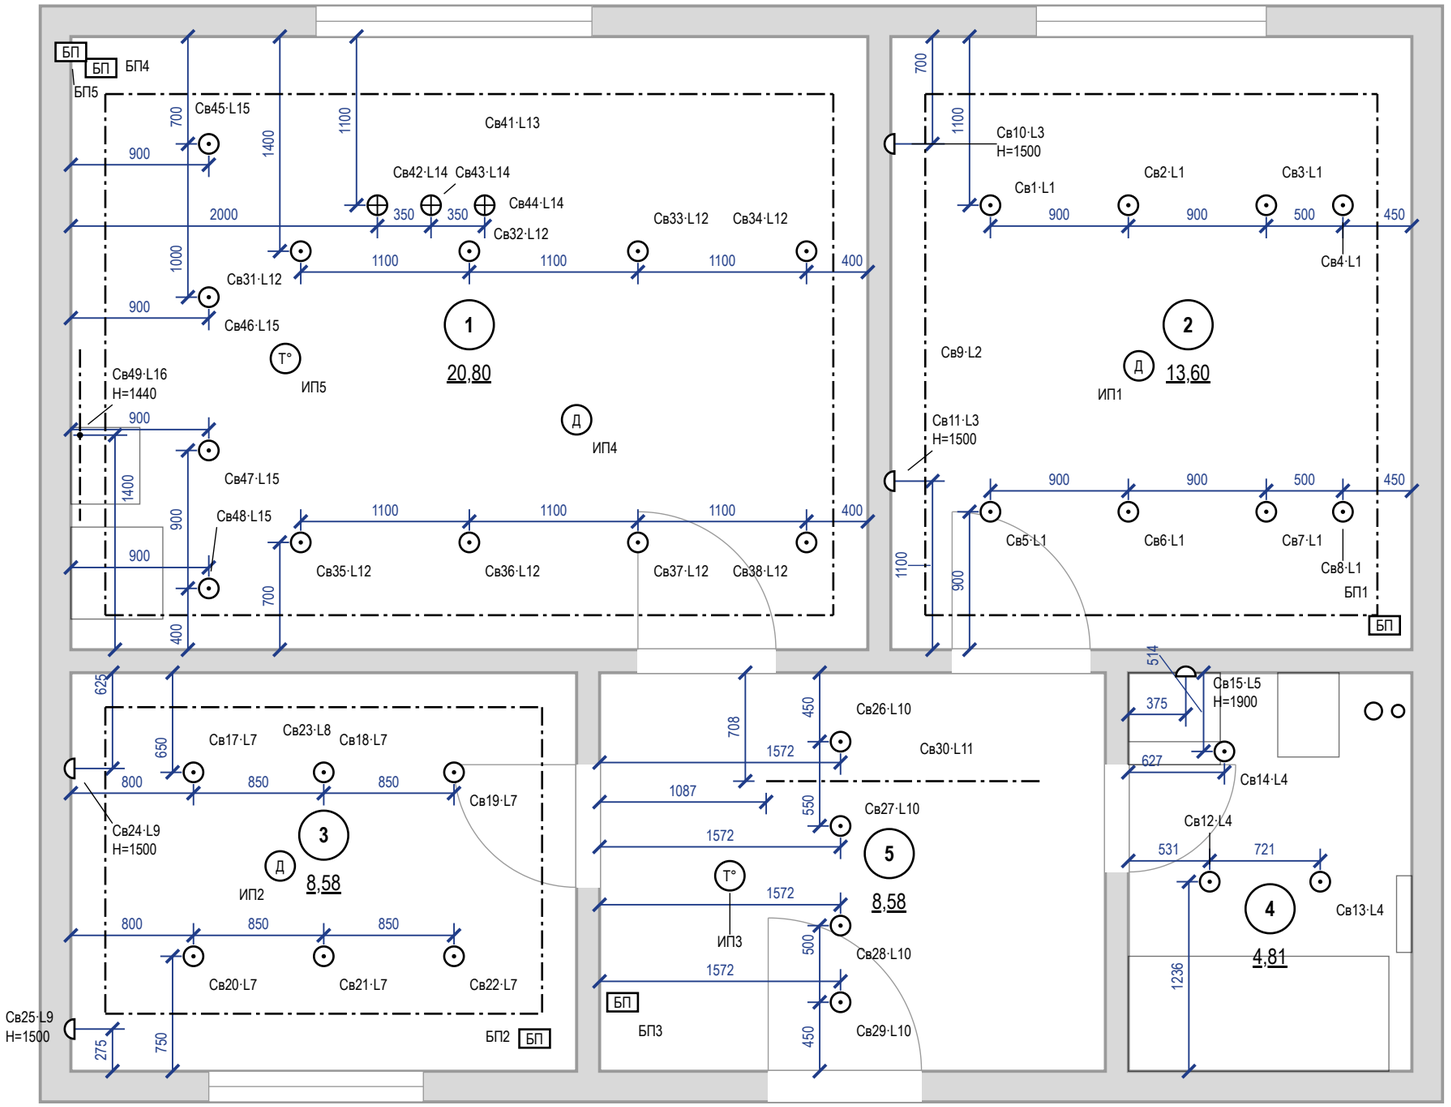

Примечания

1. За отметку 0,000 принят уровень чистого пола. Высоты H — от чистого пола до оси изделия; привязки — от чистовой грани стены до оси механизма (у рамки на несколько постов — до оси рамки).
2. Высота установки, не указанная на плане: светильники — на потолке; настенные — по отметке H у знака. Привязки — до оси светильника от чистовой грани стены, по рядам.
3. Освещённость: Eн — СанПиН 1.2.3685-21, табл. 5.52 (на полу); Ф треб. = Eн·S/(U·MF) при U = 0,5 и MF = 0,71 (СП 52.13330.2016, табл. 4.3) — оценка, не светотехнический расчёт. Декоративная подсветка в Ф не входит.
4. Во влажных помещениях — светильники не ниже IP44; в зонах 0–2 ванной — по ГОСТ Р 50571.7.701-2024 (зона 1 — IPX5).
5. LED-лента в карнизе подсветки короба — по линии карниза с плана потолков; блок питания — в люке короба (БП на плане), питание ленты длиннее 5 м — с двух концов.
6. Розеточные и мокрые линии — через УЗО или дифавтомат с током утечки не более 30 мА (ПУЭ 7.1.79); в санузле выполнить ДСУП (ПУЭ 7.1.87–7.1.88).
7. Кабель — медный, исполнение нг(A)-LS (ГОСТ 31565-2012); скрытая прокладка только горизонтально и вертикально, фактические трассы зафиксировать исполнительной схемой до закрытия отделкой.
8. Расчёт нагрузок, токов КЗ, селективности и сечений по проекту ЭОМ организации с допуском СРО; лист задаёт состав, расположение и группы.
9. Ведомость светильников — лист «Ведомость электроточек и изделий».

					Проект: Квартира 56 м²
	Лист	№ док.	Подпись	Дата	План освещения
Дизайнер	Кырлан А.С.			19.10.26	

Стадия	Лист	Листов
П	23	56

выпуск 19.10.2026 № 60226ce68e · стр. 23 из 56

Спецификация светильников

Поз.	Марки	Наименование	Установка	Кол.	P, Вт	Σ P, Вт	Ф, лм	Тц, К	Ra	Угол, °	IP	Дим.	Группа	Пом.
1	Св31–Св38	Встраиваемый точечный	в ГКЛ, корпус ≤ 70 мм	8	12	96	1000	3000	90	—	20	да	L12	1
2	Св41	Лента светодиодная 24 В	в карнизе короба, профиль с рассеивателем	16,3 м	9,6/м	156,5	900/м	2700	90	—	20	да	L13	1
3	Св42, Св43, Св44	Подвесной	подвес, низ H=1450	3	9	27	800	3000	90	—	20	да	L14	1
4	Св45–Св48	Встраиваемый точечный	в ГКЛ, корпус ≤ 70 мм	4	10	40	900	3000	90	—	20	да	L15	1
5	Св49	Линейный настенный	под верхними шкафами, H=1440	1	18	18	1500	3000	90	—	20	да	L16	1
6	Св1–Св8	Встраиваемый точечный	в ГКЛ, корпус ≤ 70 мм	8	12	96	1000	2700	90	—	20	—	L1	2
7	Св9	Лента светодиодная 24 В	в карнизе короба, профиль с рассеивателем	12,7 м	9,6/м	121,9	900/м	2700	90	—	20	да	L2	2
8	Св10, Св11, Св24, Св25	Настенный (бра)	на стене, H=1500	4	6	24	400	2700	90	60	20	—	L3, L9	2, 3
9	Св17–Св22	Встраиваемый точечный	в ГКЛ, корпус ≤ 70 мм	6	12	72	1050	2700	90	—	20	—	L7	3
10	Св23	Лента светодиодная 24 В	в карнизе короба, профиль с рассеивателем	9,7 м	9,6/м	93,1	900/м	2700	90	—	20	да	L8	3
11	Св12–Св14	Встраиваемый точечный	встраиваемый	3	6	18	500	3000	90	—	44	—	L4	4
12	Св15	Настенный светильник над зеркалом, драйвер встроен	над зеркалом, H=1900	1	8	8	600	3000	90	—	44	—	L5	4
13	Св26–Св29	Встраиваемый точечный	в ГКЛ, корпус ≤ 70 мм	4	7	28	600	3000	90	—	20	—	L10	5
14	Св30	Лента светодиодная 24 В	в коробе, профиль с рассеивателем, датчик движения	1,8 м	4,8/м	8,6	150/м	2700	90	—	20	нет	L11	5
		Итого		**42 шт + 40,5 м**		**807,2**								

Слои света по помещениям

Пом.	Помещение	Слои света и группы включения (марки светильников)	Тц, К	Ra	Σ P, Вт	Сцен.
1	Гостиная-кухня	общий — L12 (Св31–Св38), L14 (Св42, Св43, Св44), L15 (Св45–Св48); рабочий — L16 (Св49); акцентный — L13 (Св41)	2700 / 3000	90	337,5	4
2	Спальня	общий — L1 (Св1–Св8); рабочий — L3 (Св10, Св11); акцентный — L2 (Св9)	2700	90	229,9	2
3	Детская	общий — L7 (Св17–Св22); рабочий — L9 (Св24, Св25); акцентный — L8 (Св23)	2700	90	177,1	1
4	Санузел	общий — L4 (Св12–Св14); рабочий — L5 (Св15)	3000	90	26	—
5	Прихожая	общий — L10 (Св26–Св29); ночной — L11 (Св30)	2700 / 3000	90	36,6	—

Примечания

1. Позиции и марки Св — те же, что на плане освещения (лист 23) и в ведомости светильников (лист «Ведомость электроточек и изделий»); группы L — по плану выключателей (лист 25).
2. Модели светильников не назначены: подбор по графам спецификации — поток, Тц, Ra, угол, IP и диммирование не хуже указанных, мощность не больше; встраиваемые — под глубину короба (графа «Установка»). IP 20 — сухие помещения.
3. Длина LED-ленты в карнизе — по линии карниза плана потолков (лист 19); Σ P = Вт/м × длина. Блок питания загружен не больше чем на 80 %; лента 24 В длиннее 10 м питается с двух концов; доступ к блоку питания — люк ревизии 300×300 мм или место, указанное в таблице.
4. Сценарии: уровень — доля максимальной яркости группы, %; 0 — группа выключена. Уровень ниже 100 % — только у групп на светорегуляторе (задний фронт, ТЕ) с диммируемыми драйверами и блоками питания.
5. Мощность и поток — по паспортам принятых изделий, Σ P — установленная мощность освещения. Оценка освещённости — на плане освещения; это не светотехнический расчёт.

LED-ленты, линейные светильники и блоки питания

Марка	Пом.	L, м	U, В	Вт/м	Σ P, Вт	БП	P БП, Вт	Загр., %	Питание	Доступ к БП
Св41	1	16,3	24	9,6	156,5	БП4	300	52	с двух концов	люк 300×300 в коробе У1 у входа
Св49	1	3	24	—	18	БП5	60	30	встроенный ввод	в пенале М6, верх, съёмная панель
Св9	2	12,7	24	9,6	121,9	БП1	200	61	с двух концов	люк 300×300 в коробе У1 у входа
Св23	3	9,7	24	9,6	93,1	БП2	200	47	с двух концов	люк 300×300 в коробе У1 у окна
Св30	5	1,8	24	4,8	8,6	БП3	20	43	с одного конца	в шкафу М_27, верхняя полка

Сценарии освещения

Пом.	Сценарий	Группы и уровни, %	Чем включается
1	Вечер	L12 споты гостиной — 30; L13 подсветка короба — 100; L14 подвесы над столом — 50; L15 споты кухни — 0; L16 подсветка столешницы — 0	S10 светорегулятор, S11 светорегулятор
1	Ужин	L12 споты гостиной — 0; L13 подсветка короба — 60; L14 подвесы над столом — 100; L15 споты кухни — 0; L16 подсветка столешницы — 30	S10 светорегулятор, S11 светорегулятор, S12 светорегулятор
1	Кино	L12 споты гостиной — 0; L13 подсветка короба — 20; L14 подвесы над столом — 0; L15 споты кухни — 0; L16 подсветка столешницы — 0	S10 светорегулятор
1	Готовка	L12 споты гостиной — 50; L13 подсветка короба — 0; L14 подвесы над столом — 0; L15 споты кухни — 100; L16 подсветка столешницы — 100	S10 светорегулятор, S11 светорегулятор, S12 светорегулятор
2	Вечер	L1 споты — 0; L2 подсветка короба — 100; L3 бра — 100	S1, S2, S3
2	Уборка	L1 споты — 100; L2 подсветка короба — 100; L3 бра — 0	S1, S2, S3
3	Вечер	L7 споты — 0; L8 подсветка короба — 100; L9 бра — 100	S4, S5, S6

Слои света

общий — равномерный свет помещения, по норме освещённости


рабочий — местный свет задачи: столешница, зеркало, чтение у кровати

акцентный — подсветка потолка, стен и ниш; не входит в поток общего света

ночной — путь спальня → санузел: не выше 2700 K, малая яркость, датчик движения

					Проект: Квартира 56 м²	
	Лист	№ док.	Подпись	Дата	Спецификация светильников и сценарии освещения	Стадия / Лист / Листов
Дизайнер	Кырлан А.С.			19.10.26		П / 24 / 56

выпуск 19.10.2026 № 60226ce68e · стр. 24 из 56

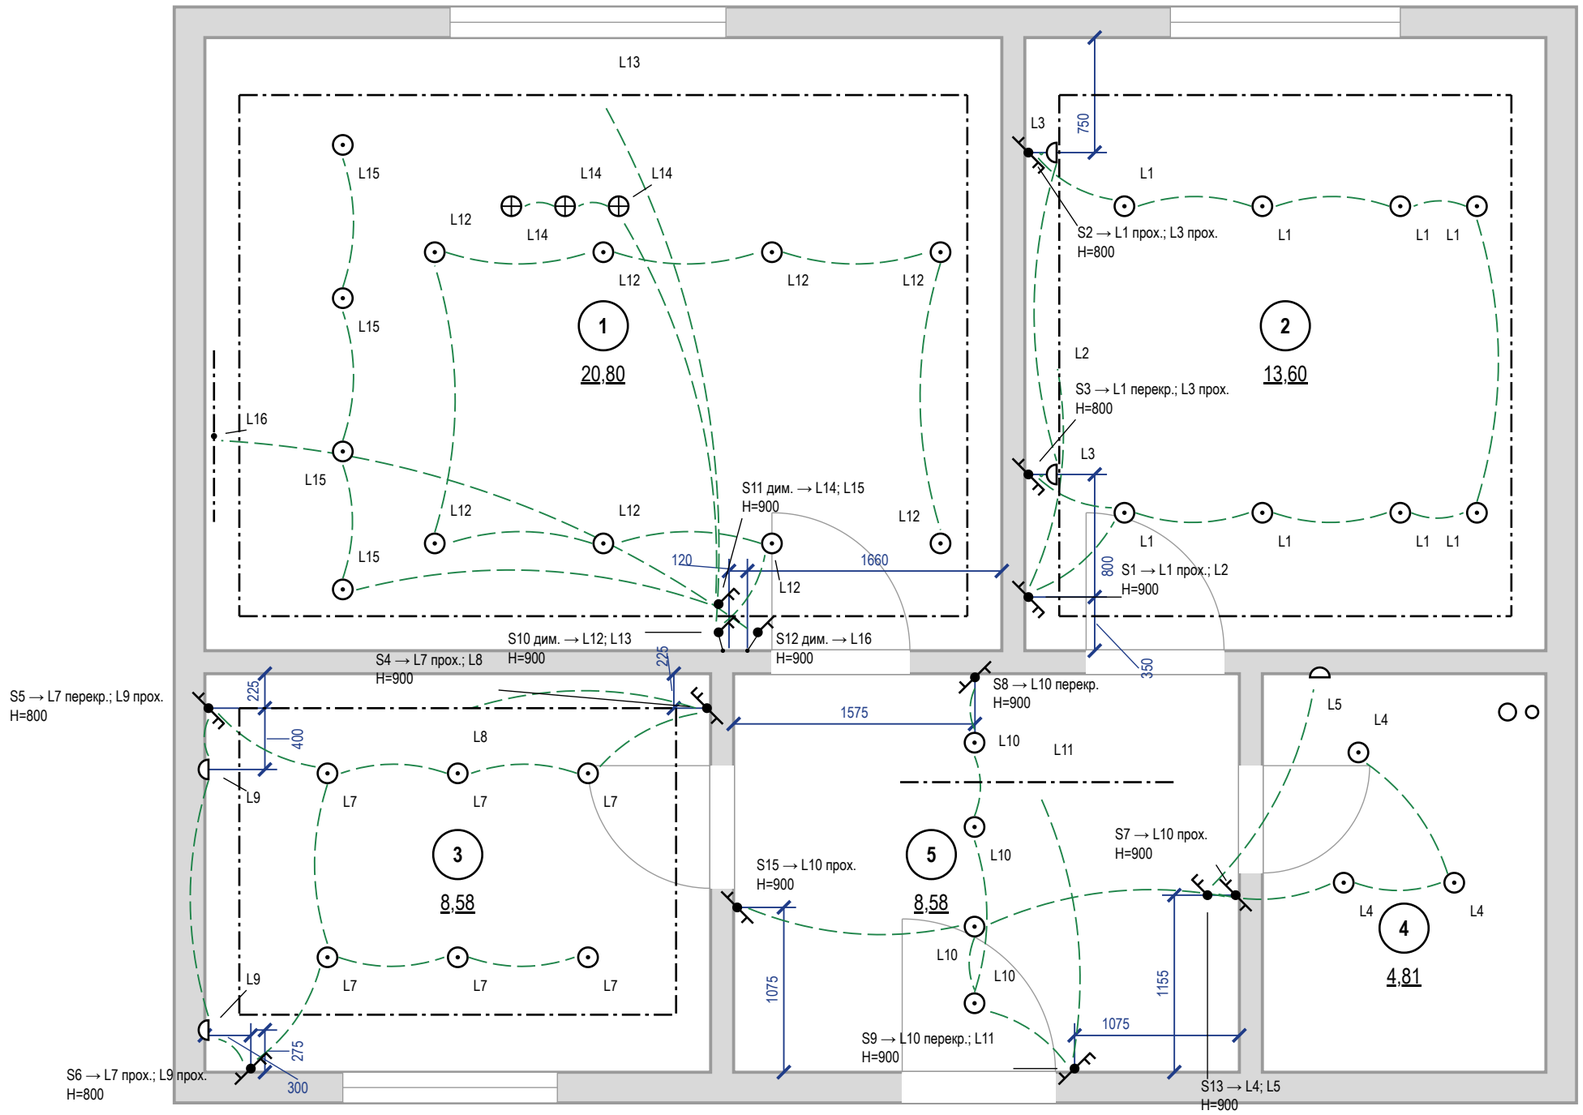


Примечания

1. За отметку 0,000 принят уровень чистого пола. Высоты H — от чистого пола до оси изделия; привязки — от чистовой грани стены до оси механизма (у рамки на несколько постов — до оси рамки).
2. Высота установки, не указанная на плане: выключатели — 900 мм от чистого пола, со стороны дверной ручки (ПУЭ 7.1.51).
3. Линии связи показывают, какой выключатель какую группу L включает; это не трасса кабеля. Трасса — принципиальная, фактическую зафиксировать исполнительной схемой.
4. Группы из нескольких мест (L1 — S1, S2, S3; L3 — S2, S3; L7 — S4, S5, S6; L9 — S5, S6; L10 — S7, S8, S9, S15): на крайних местах — проходные клавиши, на промежуточных — перекрёстные; механизмы — в ведомости изделий.
5. Светорегулятор — по заднему фронту (для LED-драйверов), совместимость с драйверами проверить до закупки.
6. Розеточные и мокрые линии — через УЗО или дифавтомат с током утечки не более 30 мА (ПУЭ 7.1.79); в санузле выполнить ДСУП (ПУЭ 7.1.87–7.1.88).
7. Кабель — медный, исполнение нг(A)-LS (ГОСТ 31565-2012); скрытая прокладка только горизонтально и вертикально, фактические трассы зафиксировать исполнительной схемой до закрытия отделкой.
8. Расчёт нагрузок, токов КЗ, селективности и сечений — по проекту ЭОМ организации с допуском СРО; лист задаёт состав, расположение и группы.
9. Расшифровка клавиш и ведомость изделий — лист «Ведомость электроточек и изделий».

					Проект: Квартира 56 м²
	Лист	№ док.	Подпись	Дата	
Дизайнер	Кырлан А.С.			19.10.26	Управление светильниками

Стадия	Лист	Листов
П	25	56

выпуск 19.10.2026 № 60226ce68e · стр. 25 из 56

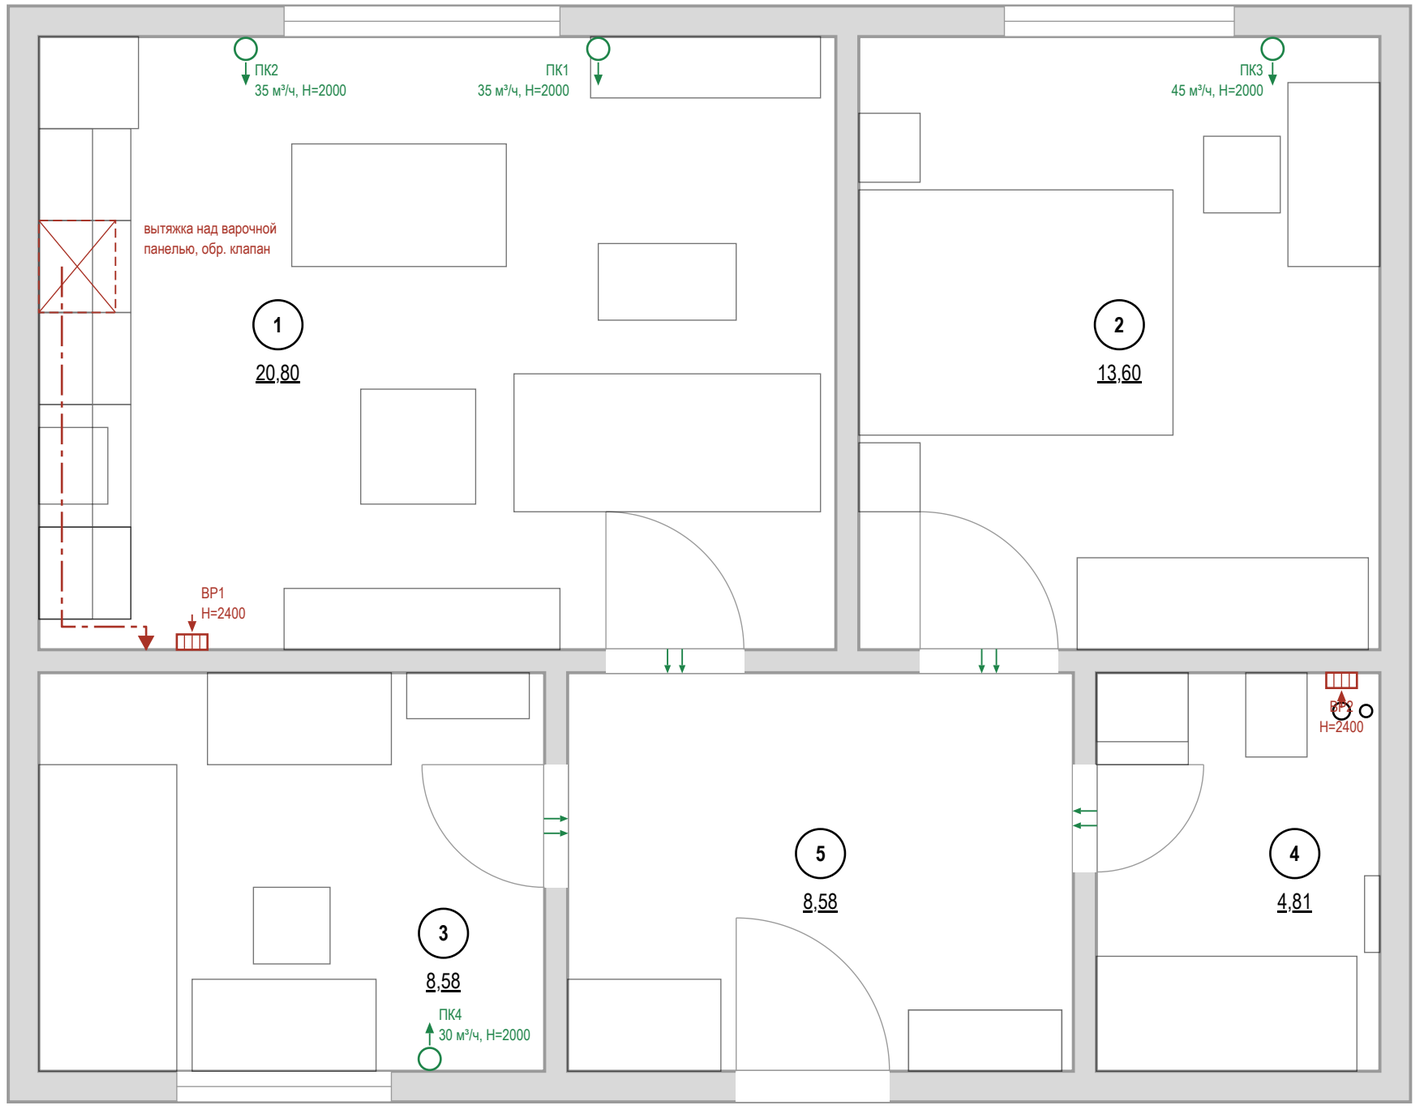

Условные обозначения

- стояк: К1 — канализация, В1 — ХВС, Т3 — ГВС
- номер помещения, площадь м²
- вытяжная решётка в вентканал: марка, расход м³/ч, Н центра от чистого пола
- приточный клапан (КИВ) в наружной стене: марка, расход, Н центра
- переток: зазор под полотном или переточная решётка
- кухонная вытяжка над варочной панелью
- воздуховод кухонной вытяжки в коробе под потолком
- отдельный вход воздуховода в вентканал, обратный клапан

Воздухообмен, м³/ч

№	Помещение	Выт. норма	Выт. проект	Прит. норма	Прит. проект	Устройства
1	Гостиная-кухня	60	60	63	70	ВР1, ПК1, ПК2
2	Спальня			41	45	ПК3
3	Детская			26	30	ПК4
4	Санузел	50	**25 !**			ВР2
	Итого	**110**	**85**	**130**	**145**	

Воздухообмен квартиры — по большей из сумм притока и вытяжки: норма 130 м³/ч, проект 145 м³/ч.
Приток больше вытяжки на 60 м³/ч — поднять вытяжку.
«!» — проект ниже нормы.


Примечания

1. Расчёт систем ОВ и подбор оборудования — проектная организация с допуском СРО; лист даёт места, трассы и привязки.
2. Нормы вытяжки — СП 54.13330.2022 (Изм. 1, 2), табл. 7.1: кухня с электроплитой 60 м³/ч, с газовой 100; ванная и совмещённый санузел 50; уборная 25; гардеробная 0,2 ч⁻¹. Приток в жилые — 3 м³/ч на 1 м² (менее 20 м² общей площади на человека), иначе 30 м³/ч на человека.
3. Вентканалы и шахты не сужать, не переносить и не закрывать; вентилятор и кухонная вытяжка — через обратный клапан, без перекрытия естественной тяги.
4. Проектные расходы — не ниже нормы, вытяжка сведена с притоком вентиляторами мокрых помещений. Клапаны — в простенке у окна, центр 2000 мм, не над кроватью, не ближе 300 мм к стоякам отопления; типоразмер — на расход.
5. Кухонная вытяжка в воздухообмен не включена: воздуховод не менее Ø125 в коробе, вход в канал отдельный.
6. Переток — зазор под полотнами межкомнатных дверей или переточная решётка.
7. Кондиционирование заданием не предусмотрено; при установке трассы фреона и дренажа (не менее 40 мм/м, в К1 через сифон) и питание заложить до черновых работ.
8. Привязки оборудования — по паспортам приобретённых моделей, до черновых работ.

					Проект: Квартира 56 м²
	Лист	№ док.	Подпись	Дата	План вентиляции
Дизайнер	Кырлан А.С.			19.10.26	

Стадия	Лист	Листов
П	26	56

выпуск 19.10.2026 № 60226ce68e · стр. 26 из 56

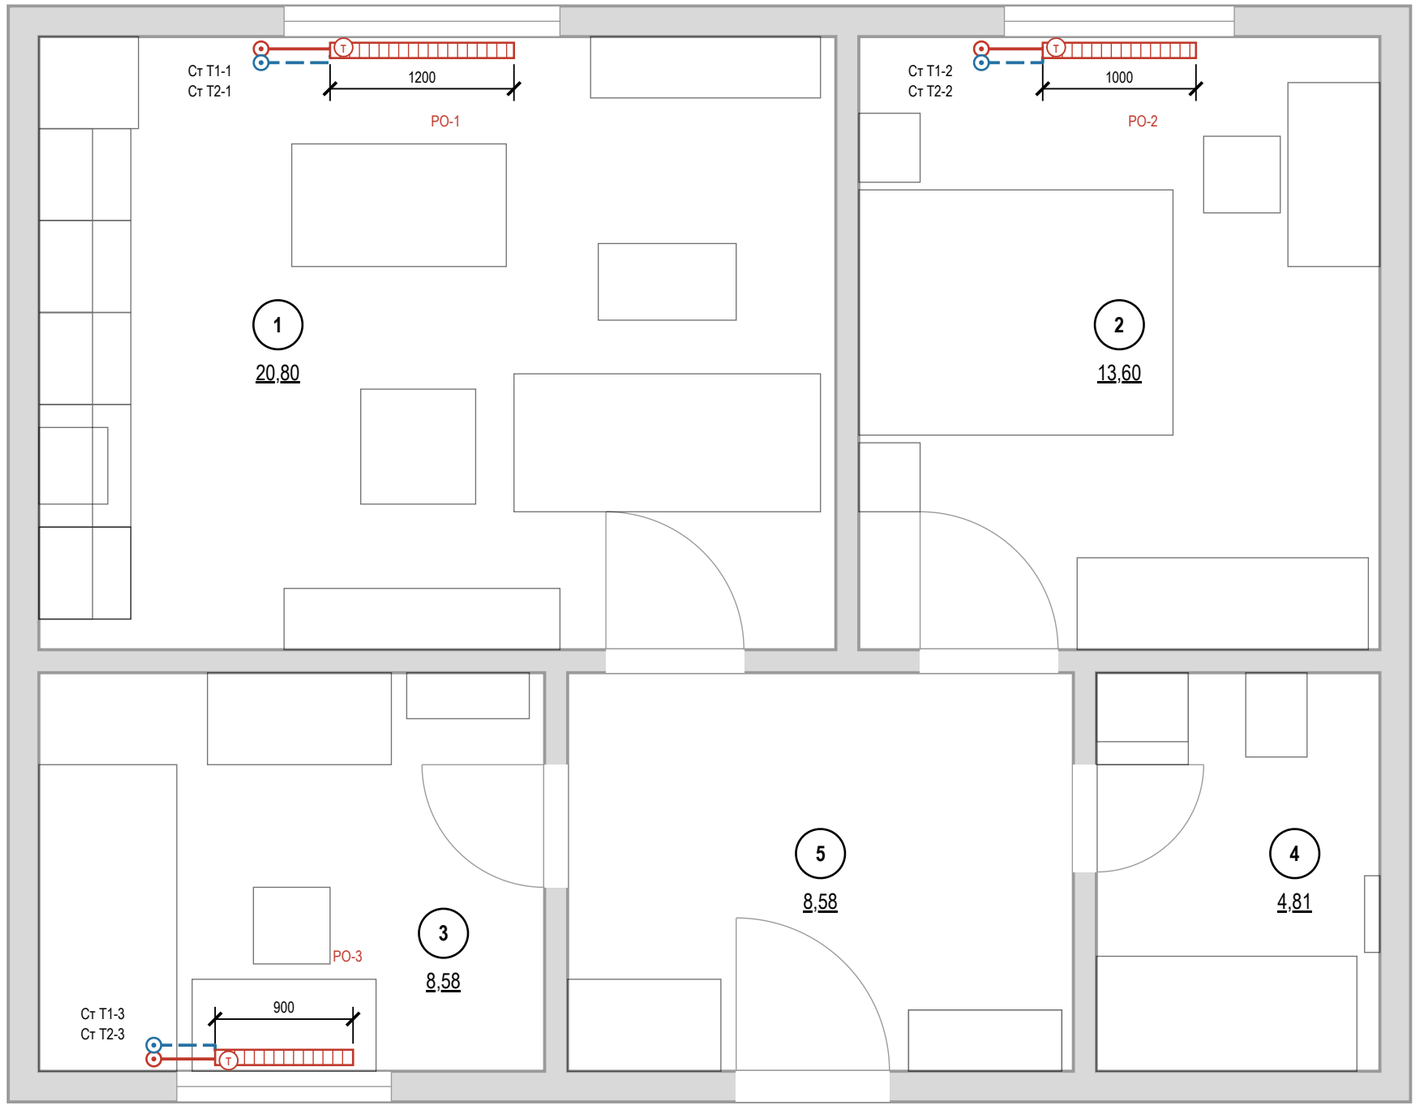

Условные обозначения

- 1 — номер помещения, площадь м²
- радиатор отопления (марка РО-N, длина по плану)
- Т — клапан с термоголовкой на подаче
- стояк отопления, подающий (Ст Т1-N)
- стояк отопления, обратный (Ст Т2-N)
- Т1 — отопление, подающий трубопровод
- Т2 — отопление, обратный трубопровод

Ведомость радиаторов

Марка	Помещение	Тип	Д×В×Г, мм	Низ / стена	Q, Вт
РО-1	1. Гостиная-кухня	панельный	1200×600×100	120 / 40	расч.
РО-2	2. Спальня	панельный	1000×600×100	120 / 40	расч.
РО-3	3. Детская	панельный	900×600×100	120 / 40	расч.

тип и мощность — по теплотехническому расчёту
Низ — от чистого пола, стена — зазор до задней панели, мм.


Привязки — до обмера
Стояки отопления в исходных данных не заданы: показаны у откосов окон, подводки — принципиально. До черновых работ — обмер стояков и паспорта приборов; лист перевыпустить по факту.

Примечания




1. Расчёт системы отопления, теплопотерь и подбор приборов — проектная организация с допуском СРО; лист даёт места и привязки.
2. Тип, длина и мощность радиаторов — по теплотехническому расчёту; лист задаёт места, зазоры и подключение.
3. Радиаторы — под каждым окном жилых комнат и кухни, центр по оси проёма, длина 0,7 ширины окна (кратно 100); окончательно — по расчёту.
4. Зазоры радиатора: низ не менее 100 мм от чистого пола, верх не менее 100 мм до подоконника, 30–50 мм от стены до задней панели; центр по оси окна с допуском ±20 мм.
5. Радиаторы не закрывать глухими коробами и мебелью; перенос и замена приборов в многоквартирном доме — переустройство, согласование с управляющей организацией (ЖК РФ ст. 25–26); вынос на лоджию запрещён.
6. Трубы отопления через межквартирные стены не прокладывать (СП 51.13330.2011, п. 9.19); через перекрытия и перегородки — в гильзах.
7. Привязки приборов и подводок — по паспортам приобретённых радиаторов и клапанов, до черновых работ.
8. До закрытия отделкой трубопроводы отопления испытать гидростатическим давлением с оформлением акта (СП 73.13330.2016, 7.2–7.3).

					Проект: Квартира 56 м²
	Лист	№ док.	Подпись	Дата	План отопления
Дизайнер	Кырлан А.С.			19.10.26	Стадия: П; Лист: 27; Листов: 56

выпуск 19.10.2026 № 60226ce68e · стр. 27 из 56

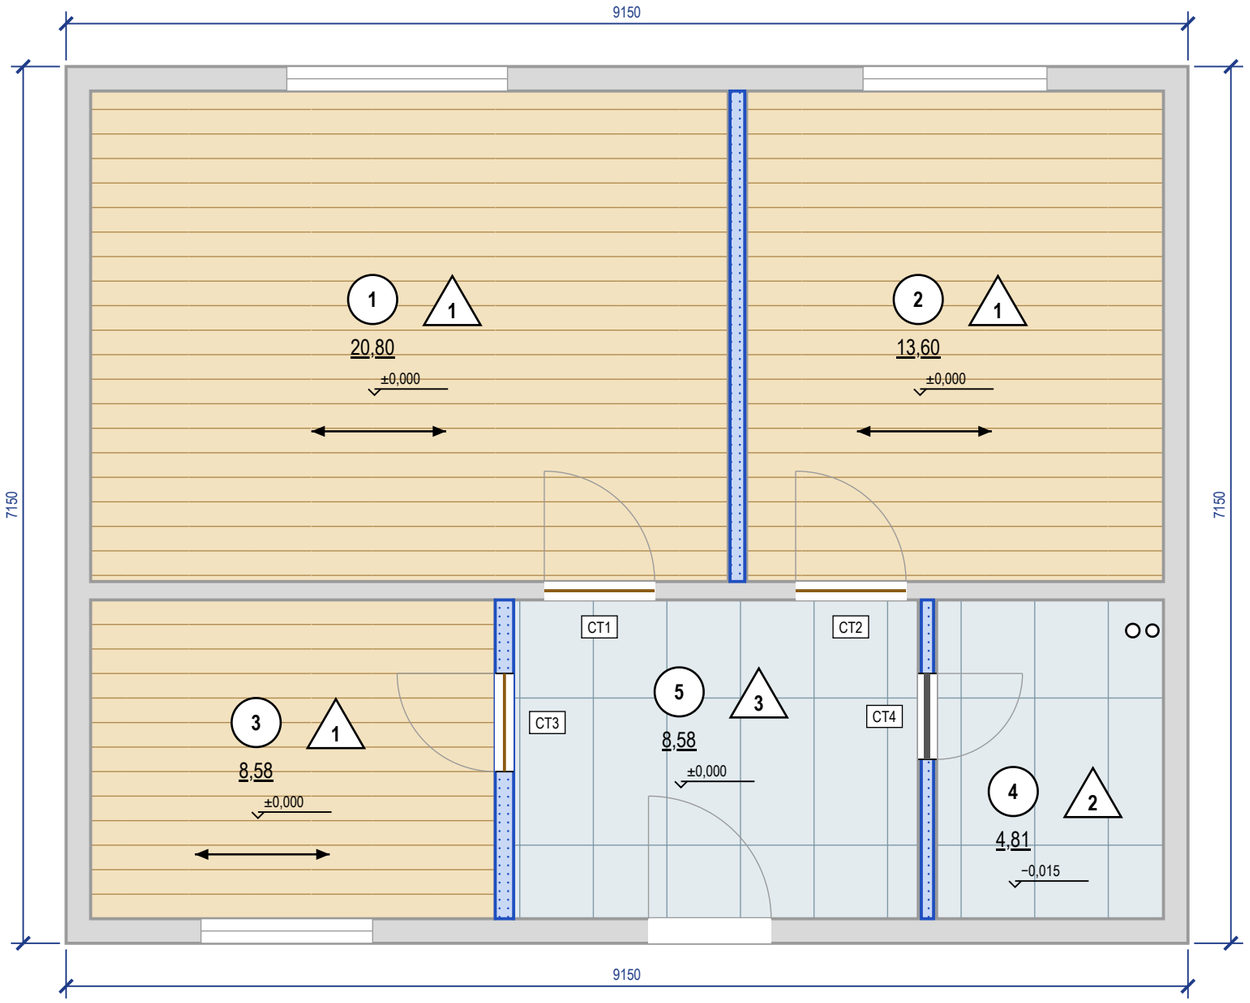

Экспликация полов

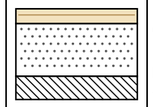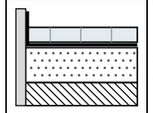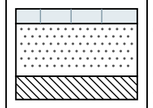Номер помещения	Тип пола	Схема пола	Данные элементов пола (наименование, толщина, основание), мм	Площадь, м²
1, 2, 3	1		Инженерная доска на клею — 14 Стяжка ЦПС М200 — 50 Плита перекрытия Всего 64 мм; ЧП ±0,000, верх плиты −0,064	42,98
4	2		Керамогранит на клею С2 TE S1 — 14 Гидроизоляция обмазочная, 2 слоя, с заведением на стены 200 мм — 2 Стяжка ЦПС М200 — 33 Плита перекрытия Всего 49 мм; ЧП −0,015, верх плиты −0,064	4,81
5	3		Керамогранит на клею С2 TE S1 — 14 Стяжка ЦПС М200 — 50 Плита перекрытия Всего 64 мм; ЧП ±0,000, верх плиты −0,064	8,58
			Итого	**56,37**

Спецификация плинтусов

Наименование	Помещения	Длина, м (с запасом)
Плинтус МДФ под покраску 80×16, крепление к стене, окраска в цвет NCS S 0804-Y30R	1, 2, 5	43
SX165, h = 69 мм, крепление к стене, окраска в цвет NCS S 0804-Y30R	3	13

Отметки по высоте

±0,000	чистый пол пом. 1–3, 5; отсчёт высот
−0,015	чистый пол пом. 4, ниже на 15 мм
−0,064	верх плиты — расчёт, не замер (задание на обмер)
сущ. пол	снимается до плиты; не замерен (задание на обмер)

Примечания


1. За отметку ±0,000 принят чистый пол, не существующий (блок отметок). Площади — по чистым размерам помещений, м²; размеры — в мм.
2. Стык разнотипных покрытий — по оси дверного полотна (под полотном в закрытом положении); решение стыка — по ведомости стыков.
3. Пол санузлов ниже смежных помещений на 15 мм за счёт меньшей толщины стяжки (верх плиты общий — по экспликации полов); гидроизоляция по стяжке с заведением на стены не менее 200 мм (СП 29.13330.2011, п. 7.2), до облицовки — тест проливом и акт скрытых работ.
4. Трубопроводы в конструкции пола не прокладываются: пирог пола 49–64 мм не вмещает выпуски канализации с уклоном — выпуски К1 ведутся по стенам над чистым полом в коробах (лист 15).
5. Звукоизоляционный слой под стяжкой проектом не предусмотрен (стяжка по плите): приведённый уровень ударного шума перекрытия с полом Lnw не более 60 дБ (СП 51.13330.2011, табл. 2) подтвердить по данным дома; при превышении — плавающая стяжка по звукоизоляции с демпферной лентой по контуру и у стояков, пирог пересчитать.
6. Штучные покрытия (инженерная доска): направление — по стрелке; влажность основания по СМ не более 2,0 % (по ТУ изготовителя).
7. Ровность основания — просвет под 2-метровой рейкой не более 2 мм: пом. 1, 2, 3 (инженерная доска), пом. 4, 5 (керамогранит); проверить до укладки покрытия (СП 71.13330.2017, табл. 8.5).
8. Сетка на плитке — условная, в размер формата; точка старта и раскладка — по листу раскладки плитки.
9. Пироги полов — по экспликации полов: слои сверху вниз, толщины в мм; гидроизоляция мокрых зон — в пироге и в ведомости отделки; схема пола — без масштаба.

					Проект: Квартира 56 м²
	Лист	№ док.	Подпись	Дата	
Дизайнер	Кырлан А.С.			19.10.26	План покрытий пола

Стадия	Лист	Листов
П	28	56

выпуск 19.10.2026 № 60226ce68e · стр. 28 из 56

Фрагмент 1. Санузел (пом. 4). Пол 600×600, шов 2 мм, М 1:20

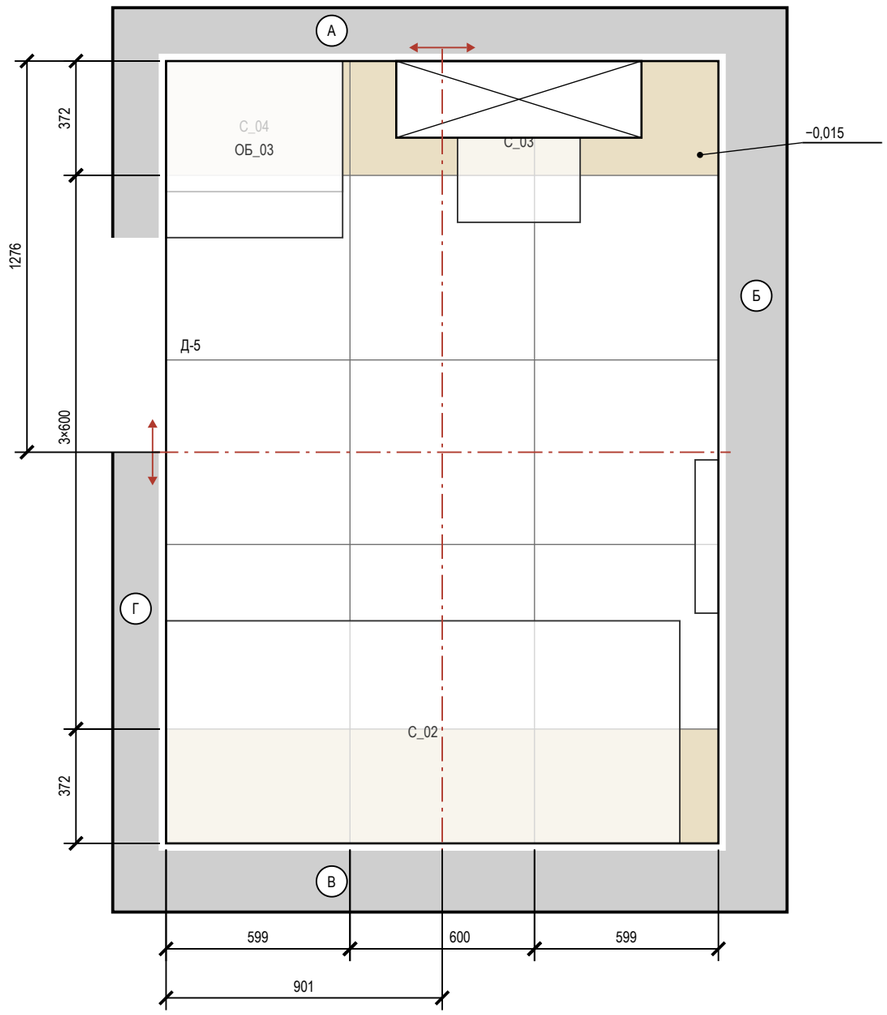

Ведомость плитки

Помещение, поверхность	Плитка, код	Формат	Шов	S, м²	Целых	Подр.	С запасом
Санузел, пол	аналог: керамогранит под травертин	600×600	2	4,81	9	6	17
Санузел, стены А–Г	аналог: керамогранит под травертин	600×1200	2	18,97	18	14	36
Санузел, короб инсталляции	аналог: керамогранит под травертин	600×1200	2	1,76	0	6	7
Прихожая, пол	A8UZ	600×1200	2	8,58	4	14	20
Гостиная-кухня, фартук (ст. Г)	аналог: керамогранит под травертин, матовый	1200×600	2	1,82	0	5	6
Итого 600×600				4,81	9	6	17
Итого 600×1200				**31,13**	**22**	**39**	**69**

Ведомость материалов

Материал	Класс, код	Норма расхода	Кол-во
Затирка	CG2WA Mapei Ultracolor Plus 132	(a+b)/ab·шов·t·1,6	2,1 кг
Затирка	CG2WA	(a+b)/ab·шов·t·1,6	0,8 кг
Клей	C2 TE S1 Ceresit CM 17	1,5 кг/м²·мм, слой 5	204 кг (9 меш.)
Клей	C2 TE S1	1,5 кг/м²·мм, слой 5	85 кг (4 меш.)
Гидроизоляция	обмазочная, 2 слоя: пол, стены по периметру и зоны замачивания	по ТУ	12,4 м²
Демпф. лента	по периметру пола из плитки		16,9 м

Условные обозначения

- плитка целая; тонкая линия — шов
- плитка с подрезкой (размер — на цепочке)
- ось старта; стрелки — направление укладки
- сантехприбор: габарит, высота по практике
- короб инсталляции: плитка пола — до короба
- отметка чистого пола на полке выноски, м
- (А) обозначение стены А–Г (как на развёртках)


Примечания

1. Раскладка от чистовых размеров: стены санузлов теряют 10 + 5 + 9 = 24 мм на сторону (штукатурка, клей, плитка); подрезки — чистые, без шва.
2. Старт — от центра помещения (штрихпунктир, стрелки — направление укладки); размер старта — от чистовых стен Г и А.
3. Раскладка пола «Прихожая» и фартука «Гостиная-кухня» — на листе «Раскладка плитки. Прихожая. Фартук кухни».
4. Калибр партии не задан — до укладки замерить (рабочий размер W, ГОСТ 13996-2019) и пересчитать подрезки.
5. Количество: целые по раскладке + по одной на подрезку, запас 10 %; один артикул — одна партия и тон. Исключены поддон, короб, проёмы и места за коробом; S — по чистым граням: стены нетто = зона облицовки по ведомости отделки − место за коробом инсталляции 0,96 м² (плитку за коробом не кладут), короб — отдельной строкой.
6. Клей C2 TE S1 Ceresit CM 17; C2 TE S1 (ГОСТ Р 56387-2018), затирка CG2WA Mapei Ultracolor Plus 132; CG2WA; расход — по ТУ выбранной марки.
7. Гидроизоляция: пол и стены 200 мм от ЧП; над ванной — до 2000 и 300 мм за борт (см. развёртки); акт скрытых работ, пролив 24 ч.
8. Швы пола совмещены со швами стены А; по периметру — демпферная лента.
9. Отметка чистого пола −0,015, порог 15 мм; стык с соседним покрытием — по оси полотна двери.


					Проект: Квартира 56 м²
	Лист	№ док.	Подпись	Дата	Раскладка плитки. Планы полов
Дизайнер	Кырлан А.С.			19.10.26	Стадия: П; Лист: 29; Листов: 56

выпуск 19.10.2026 № 60226ce68e · стр. 29 из 56

Фрагмент 1. Прихожая (пом. 5). Пол 600×1200, шов 2 мм, М 1:25

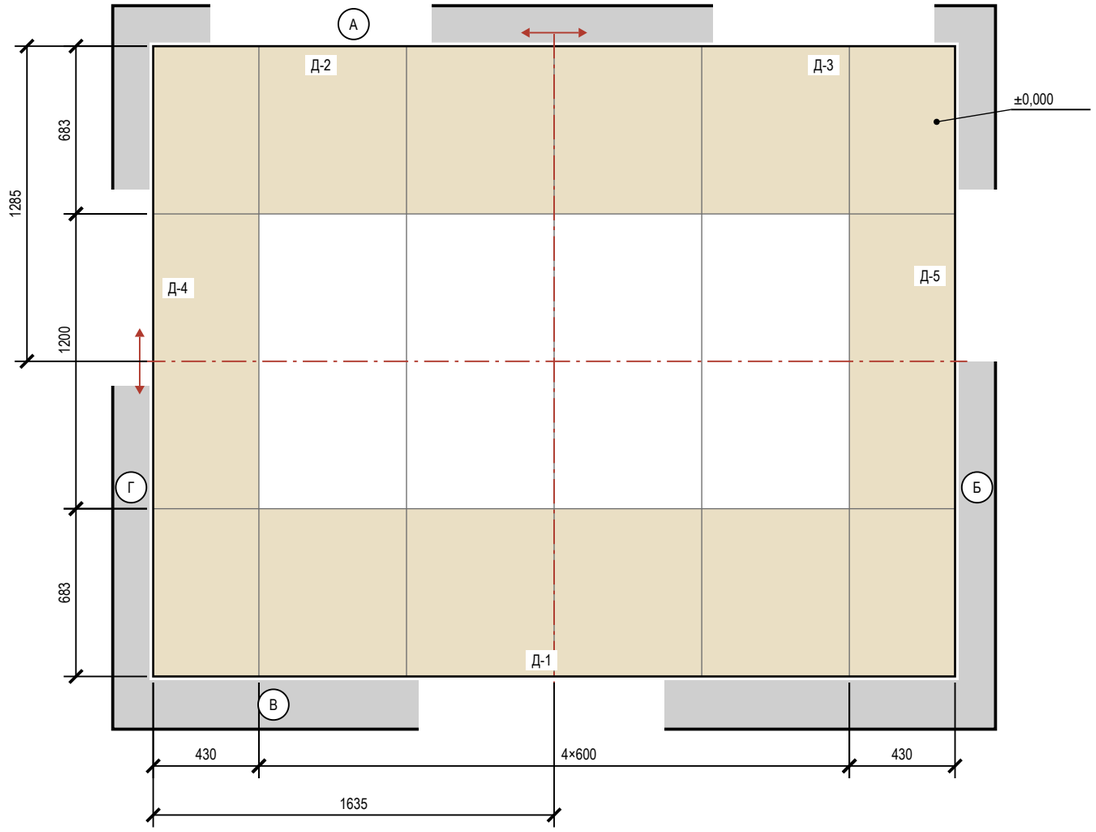

Фрагмент 2. Гостиная-кухня (пом. 1), фартук, стена Г. 1200×600, шов 2 мм, М 1:25

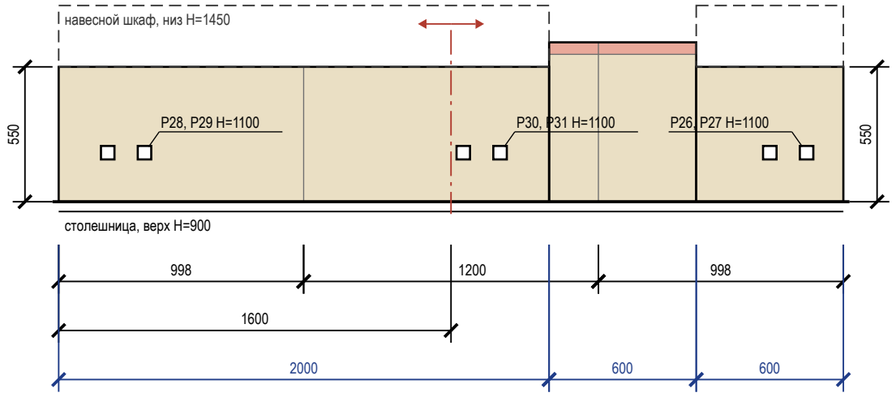

Условные обозначения

- плитка целая; тонкая линия — шов
- плитка с подрезкой (размер — на цепочке)
- ось старта; стрелки — направление укладки
- электроточка: марка и H — по листам ЭОМ
- столешница (верх)
- навесной шкаф над фартуком
- отметка чистого пола на полке выноски, м
- (А) обозначение стены А–Г (как на развёртках)

Подсчёт плитки

Поверхность	Формат	S, м²	Целых	Подр.	С запасом
Прихожая, пол	600×1200	8,58	4	14	20
Гостиная-кухня, фартук (ст. Г)	1200×600	1,82	0	5	6

Сдвиг розеток фартука под раскладку

Точка (ЭОМ)	Проект: от угла / H	Под раскладку: от угла / H	Сдвиг, мм
P26, P27, P30, P31	3050, 2900, 1800, 1650 / 1100	3050, 2900, 1800, 1650 / 1175	H +75 — ось ряда
P28, P29	350, 200 / 1100	350, 200 / 1175	H +75 — ось ряда

Примечания

1. Прихожая: керамогранит 600×1200, длинная сторона — вдоль стен Б и Г, шов 2 мм, прямая раскладка от центра. Стены окрашены: раскладка от чистового контура минус штукатурка и шпаклёвка 15 мм на сторону (принято); подрезки 430 / 683 мм, срез — под плинтус.
2. Прихожая: деформационный зазор по периметру 8–10 мм под плинтусом; в проёмах — стык с соседним покрытием по оси полотна двери. Клей C2 TE S1, затирка CG2WA.
3. Фартук, Гостиная-кухня: 1200×600 горизонтально, шов 2 мм; зоны 600 мм — 900…1450, 600 мм — 900…1550, 2000 мм — 900…1450 (от столешницы до низа навесного шкафа, без шкафа — 650 мм). Старт от центра участка, подрезки 998 мм. Площадь 1,82 м² — как в ведомости отделки.
4. Фартук — после монтажа столешницы, низ на 2–3 мм выше неё, шов со столешницей — санитарный герметик; навесные шкафы — после фартука. Торцы у пенала и стены — профиль или запил 45°.
5. Фартук, Гостиная-кухня: в зоне до отм. 1550 верхний ряд подрезан 48 мм — меньше 1/3 плитки; полоса прикрыта корпусом навесного модуля и на виду не остаётся. Раскладкой не снимается: убрать подрезку можно, только выровняв низ этого модуля с соседними (1450 мм) — решение мебельщика.
6. Розетки из таблицы переносятся до черновой электрики: по высоте — на ось ряда плитки, от вертикального шва крупной плитки — не ближе 60 мм. Привязка — от левого края фартука на развёртке.
7. Клей, затирка и итог по форматам — в ведомостях листа «Раскладка плитки. Планы полов».

					Проект: Квартира 56 м²
	Лист	№ док.	Подпись	Дата	
Дизайнер	Кырлан А.С.			19.10.26	Раскладка плитки. Прихожая. Фартук кухни

Стадия	Лист	Листов
П	30	56

выпуск 19.10.2026 № 60226ce68e · стр. 30 из 56

Развёртка стены Г


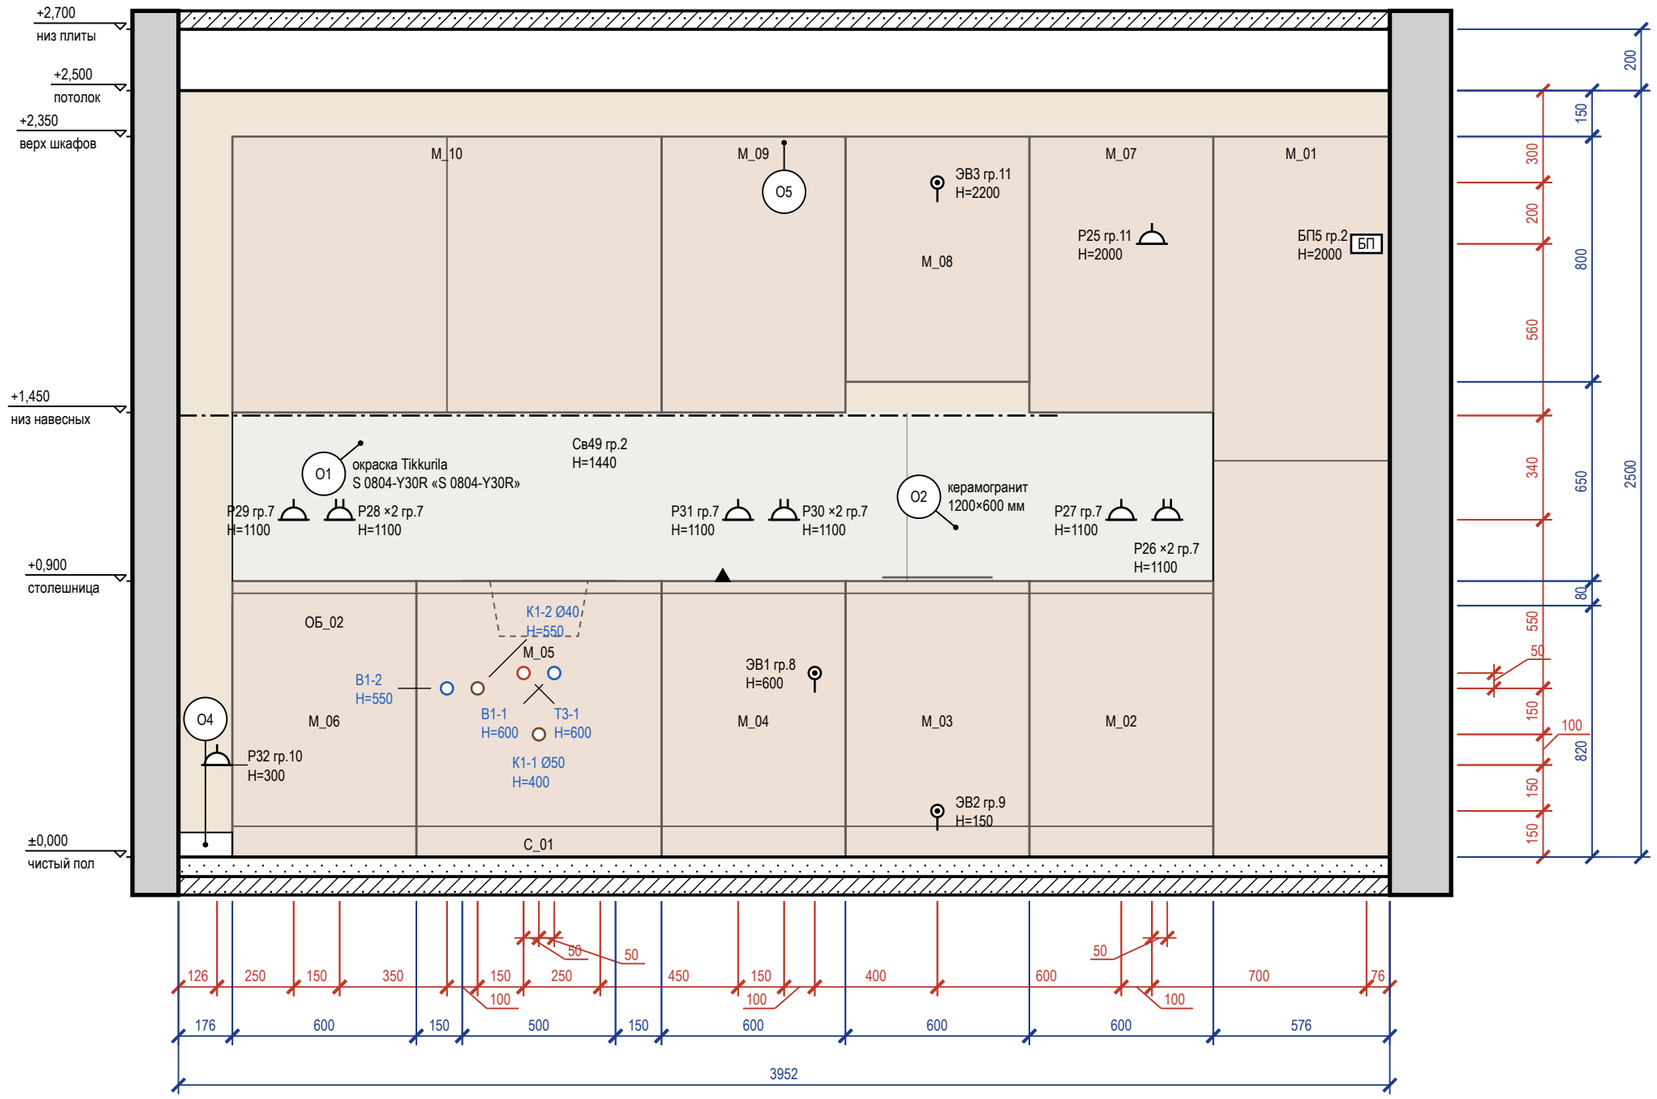


Схема развёрток (М 1:100)

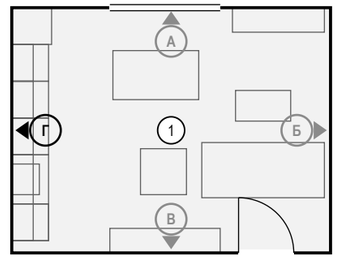

Ведомость отделки (на листе)

Марка	Поверхность	Материал, изделие	Цвет, код	Кол.
O1	стены	окраска, Tikkurila Euro Power 7, колеровка по NCS, матовая, подготовка Q3	NCS S 0804-Y30R «S 0804-Y30R»	8,1 м²
O2	фартук	керамогранит, 1200×600×9 мм, аналог: керамогранит под травертин, матовый, затирка CG2WA		1,8 м²
O4	плинтус	плинтус МДФ, h 80 мм, аналог: плинтус МДФ под покраску 80×16	NCS S 0804-Y30R «S 0804-Y30R»	0,2 м
O5	потолок	окраска, Tikkurila Euro Power 7, глубокоматовая, подготовка Q3	Tikkurila F485 «Damask»	20,8 м²

Примечания

1. Размеры — в мм от чистовых поверхностей стен; условные обозначения и общие указания — лист 2.
2. Схема мебели, приборов и декора не является технической документацией для производства мебели; габариты — по паспортам изделий.
3. Выводы ВК — коды и высоты по листу выводов сантехники.
4. Выводы кухонной техники — по утверждённому проекту кухни: привязки выводов даются от осей модулей гарнитура.
5. Потолок на развёртках — по нижнему уровню У1; другие уровни потолка помещения: У2 +2,600.

					Проект: Квартира 56 м²
	Лист	№ док.	Подпись	Дата	Развёртка стены Г. Гостиная-кухня (пом. 1), кухонный фронт
Дизайнер	Кырлан А.С.			19.10.26	

Стадия	Лист	Листов
П	31	56

выпуск 19.10.2026 № 60226ce68e · стр. 31 из 56

Развёртка стены А


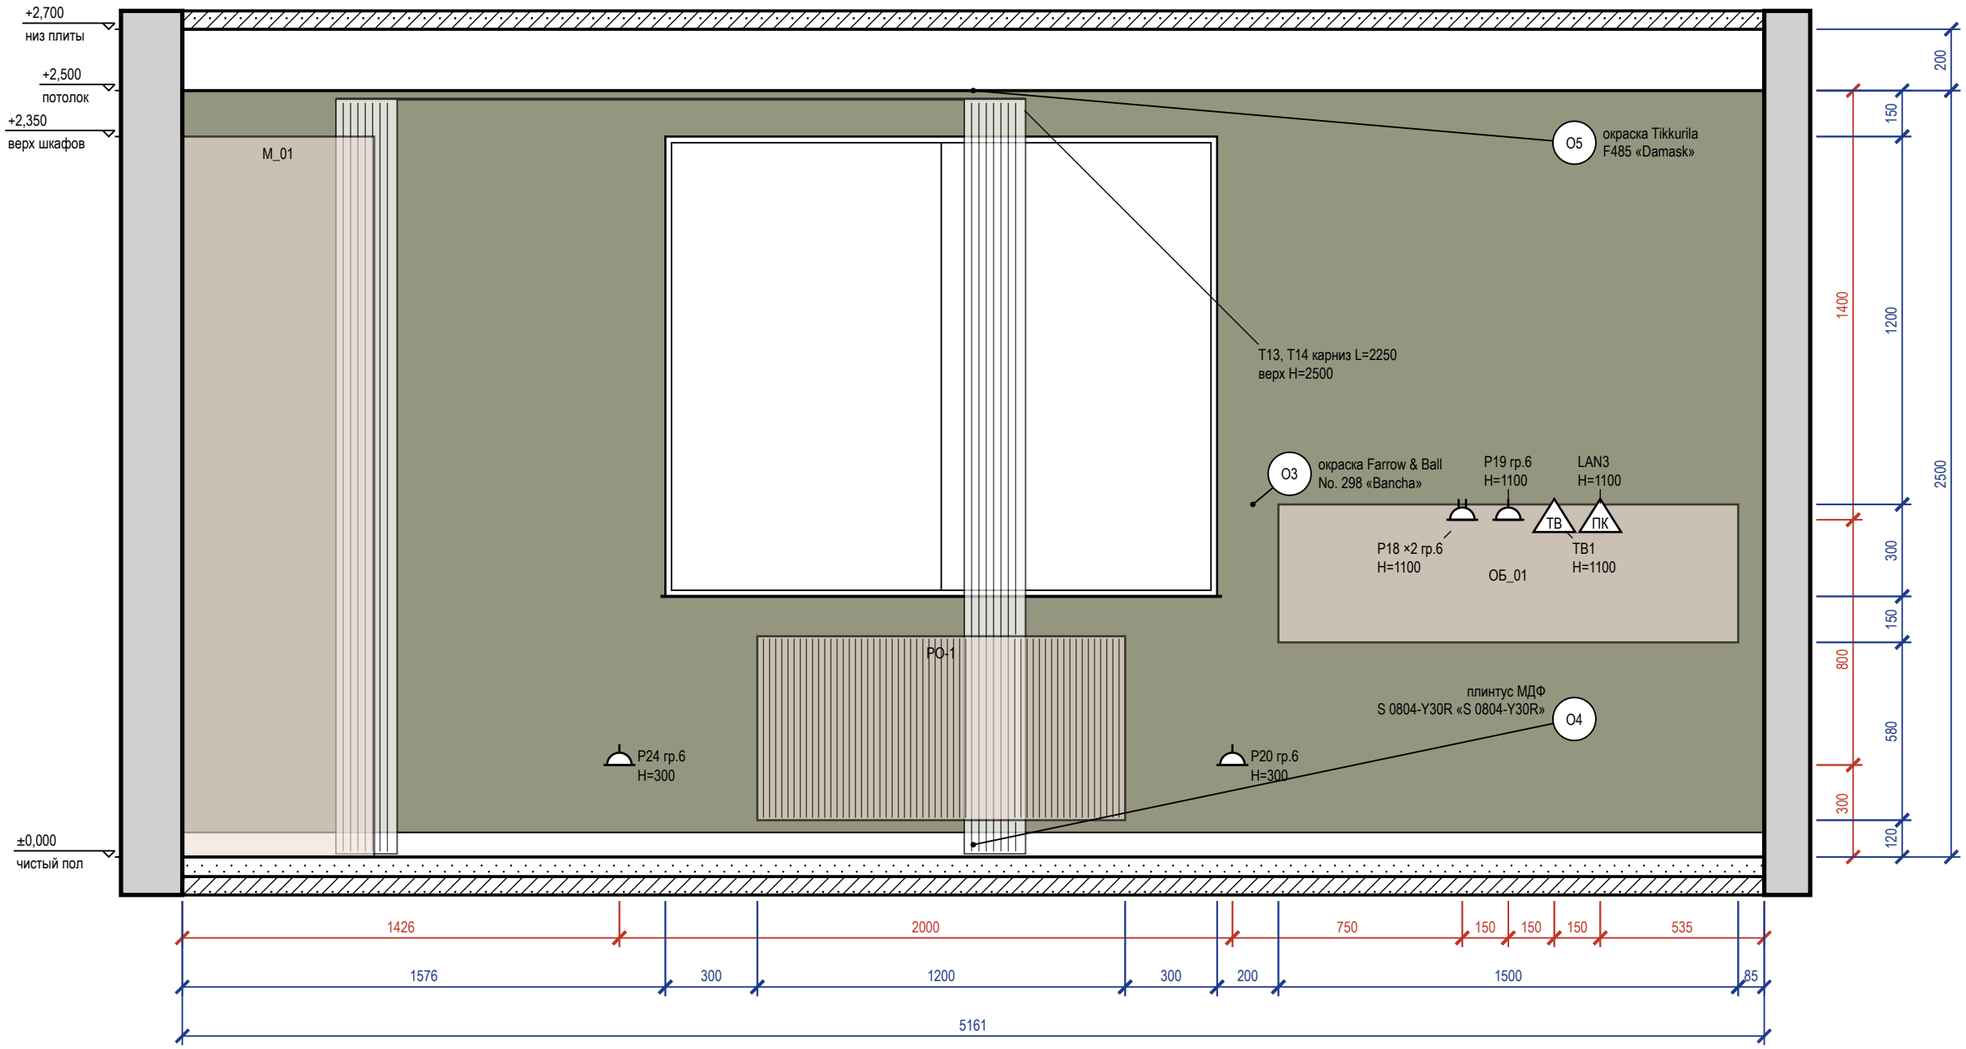


Схема развёрток (М 1:100)

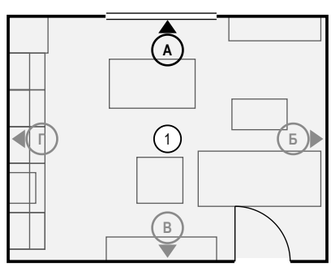

Ведомость отделки (на листе)

Марка	Поверхность	Материал, изделие	Цвет, код	Кол.
О3	акцентная стена	окраска, Farrow & Ball Modern Emulsion, матовая, подготовка Q3	Farrow & Ball No. 298 «Bancha»	10,2 м²
О4	плинтус	плинтус МДФ, h 80 мм, аналог: плинтус МДФ под покраску 80×16	NCS S 0804-Y30R «S 0804-Y30R»	5,2 м
О5	потолок	окраска, Tikkurila Euro Power 7, глубокоматовая, подготовка Q3	Tikkurila F485 «Damask»	20,8 м²

Примечания

1. Размеры — в мм от чистовых поверхностей стен; условные обозначения и общие указания — лист 2.
2. Схема мебели, приборов и декора не является технической документацией для производства мебели; габариты — по паспортам изделий.
3. Карнизы (шины) — по ведомости текстиля декоратора; длина L и верх H — по развёртке, крепление — до окраски потолка.
4. Потолок на развёртках — по нижнему уровню У1; другие уровни потолка помещения: У2 +2,600.
5. Линии узора (швы плитки, складки штор, рёбра радиаторов) прерываются у знаков и выносок — просвет между линиями не менее 0,7 мм.

					Проект: Квартира 56 м²
	Лист	№ док.	Подпись	Дата	
Дизайнер	Кырлан А.С.			19.10.26	Развёртка стены А. Гостиная-кухня (пом. 1)

Стадия	Лист	Листов
П	32	56

выпуск 19.10.2026 № 60226ce68e · стр. 32 из 56

Развёртка стены Б


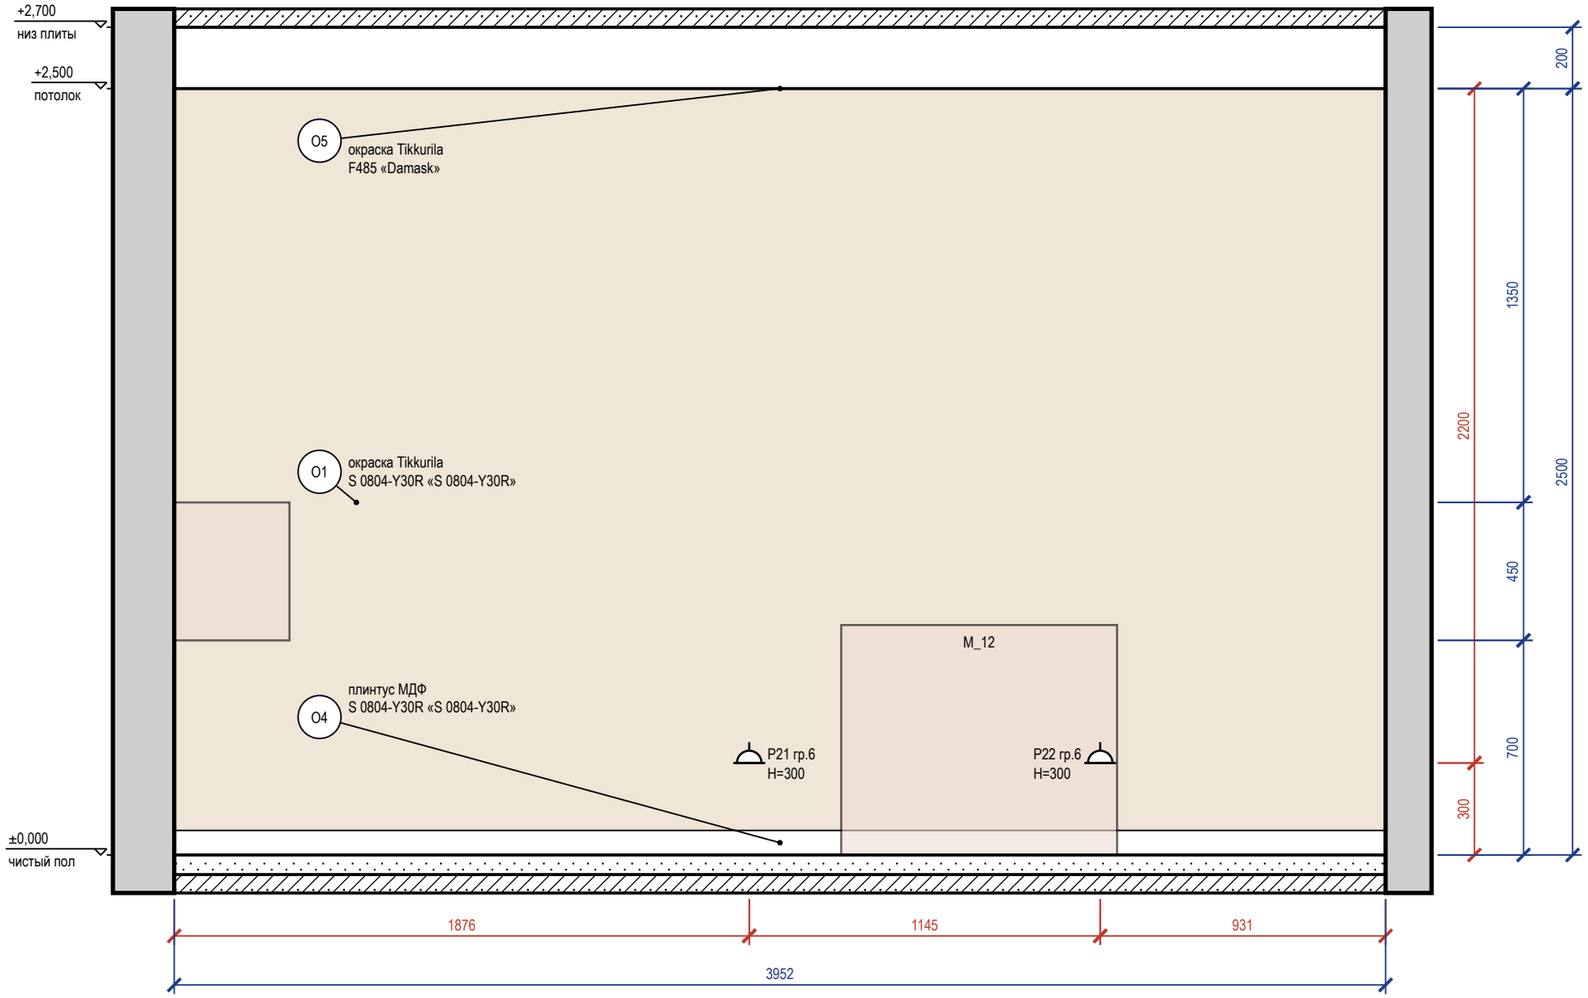


Схема развёрток (М 1:100)

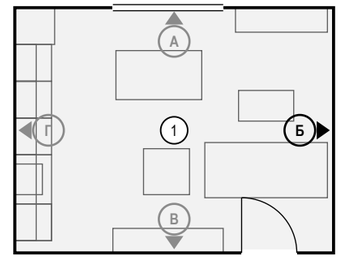

Ведомость отделки (на листе)

Марка	Поверхность	Материал, изделие	Цвет, код	Кол.
О1	стены	окраска, Tikkurila Euro Power 7, колеровка по NCS, матовая, подготовка Q3	NCS S 0804-Y30R «S 0804-Y30R»	9,9 м²
О4	плинтус	плинтус МДФ, h 80 мм, аналог: плинтус МДФ под покраску 80×16	NCS S 0804-Y30R «S 0804-Y30R»	4 м
О5	потолок	окраска, Tikkurila Euro Power 7, глубокоматовая, подготовка Q3	Tikkurila F485 «Damask»	20,8 м²

Примечания

1. Размеры — в мм от чистовых поверхностей стен; условные обозначения и общие указания — лист 2.
2. Схема мебели, приборов и декора не является технической документацией для производства мебели; габариты — по паспортам изделий.
3. Потолок на развёртках — по нижнему уровню У1; другие уровни потолка помещения: У2 +2,600.

					Проект: Квартира 56 м²
	Лист	№ док.	Подпись	Дата	
Дизайнер	Кырлан А.С.			19.10.26	Развёртка стены Б. Гостиная-кухня (пом. 1)

Стадия	Лист	Листов
П	33	56

выпуск 19.10.2026 № 60226ce68e · стр. 33 из 56

Развёртка стены В


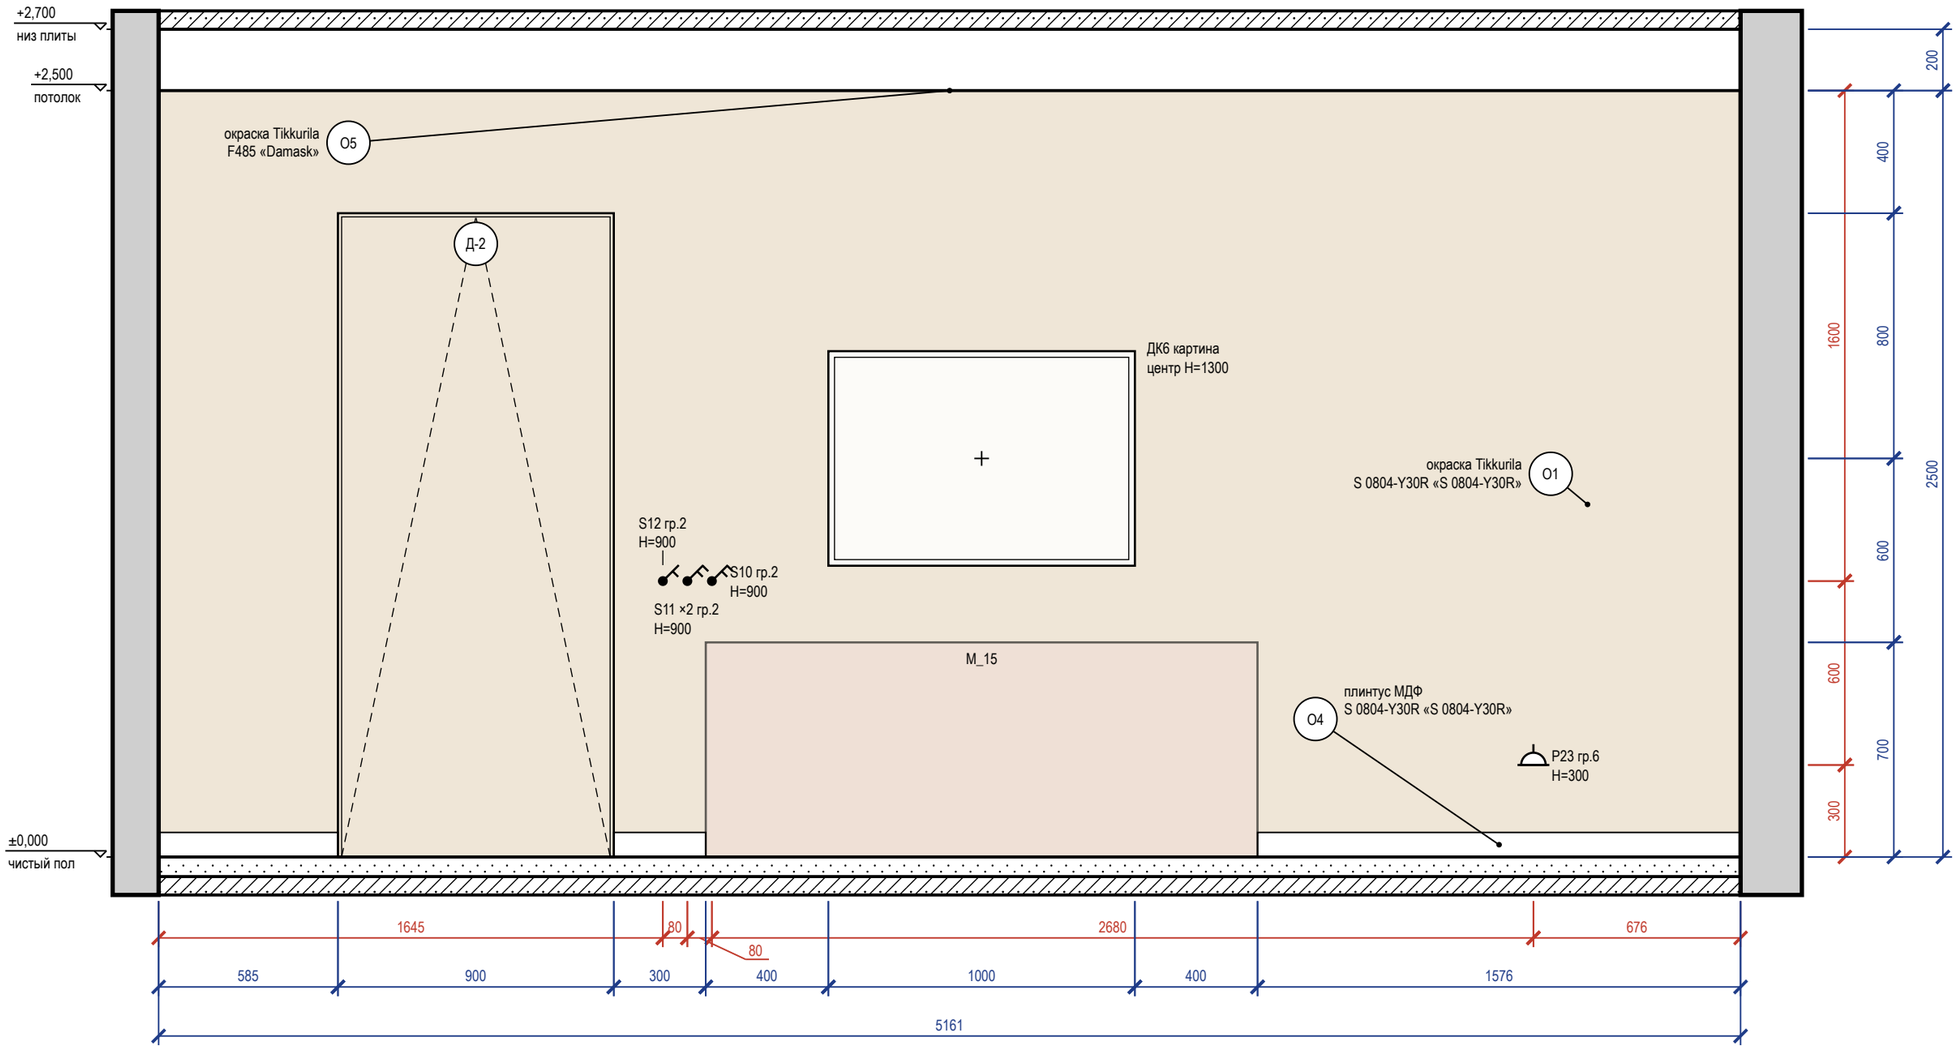


Схема развёрток (М 1:100)

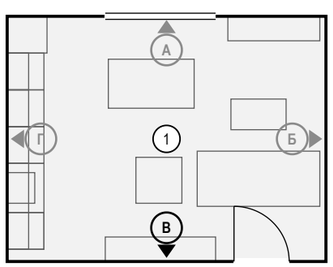

Ведомость отделки (на листе)

Марка	Поверхность	Материал, изделие	Цвет, код	Кол.
О1	стены	окраска, Tikkurila Euro Power 7, колеровка по NCS, матовая, подготовка Q3	NCS S 0804-Y30R «S 0804-Y30R»	11 м²
О4	плинтус	плинтус МДФ, h 80 мм, аналог: плинтус МДФ под покраску 80×16	NCS S 0804-Y30R «S 0804-Y30R»	2,5 м
О5	потолок	окраска, Tikkurila Euro Power 7, глубокоматовая, подготовка Q3	Tikkurila F485 «Damask»	20,8 м²

Примечания

1. Размеры — в мм от чистовых поверхностей стен; условные обозначения и общие указания — лист 2.
2. Картины и зеркала крепить к основанию по паспорту изделия (закладные и анкеры — в перечне скрытых работ); крест — ось центра предмета.
3. Двери скрытого монтажа — полотно в плоскости стены, отделка стены по полотну, плинтус прерывается у короба (узел — на листе узлов).
4. Потолок на развёртках — по нижнему уровню У1; другие уровни потолка помещения: У2 +2,600.

					Проект: Квартира 56 м²
	Лист	№ док.	Подпись	Дата	Развёртка стены В. Гостиная-кухня (пом. 1)
Дизайнер	Кырлан А.С.			19.10.26	

Стадия	Лист	Листов
П	34	56

выпуск 19.10.2026 № 60226ce68e · стр. 34 из 56

Развёртка стены А


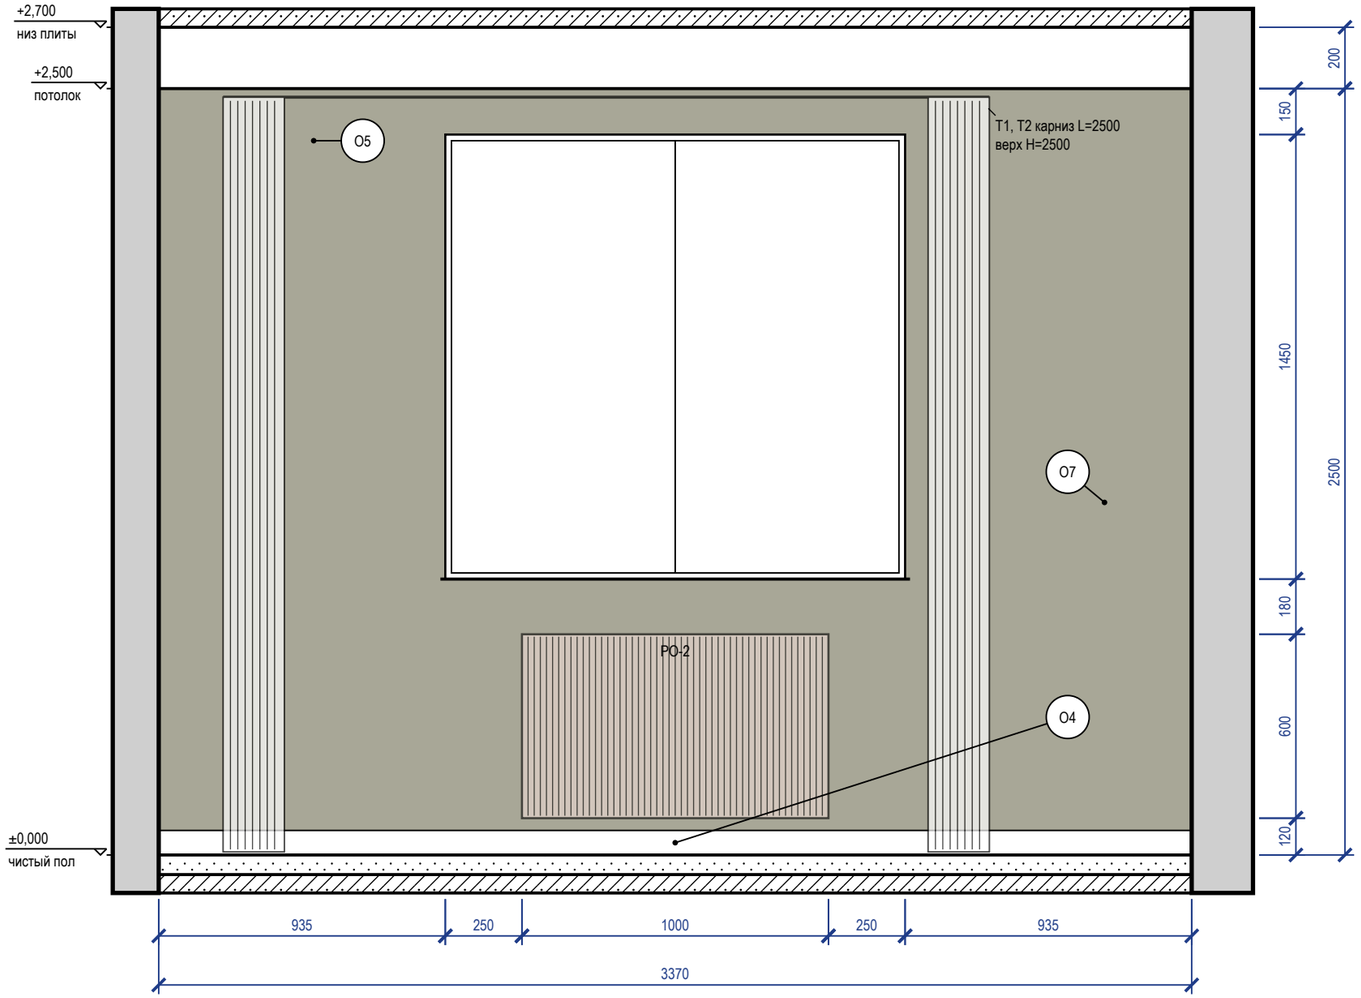


Схема развёрток (М 1:100)

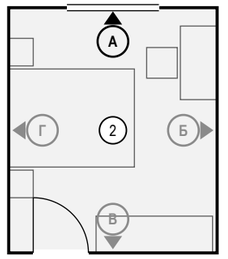

Ведомость отделки (на листе)

Марка	Поверхность	Материал, изделие	Цвет, код	Кол.
О4	плинтус	плинтус МДФ, h 80 мм, аналог: плинтус МДФ под покраску 80×16	NCS S 0804-Y30R «S 0804-Y30R»	3,4 м
О5	потолок	окраска, Tikkurila Euro Power 7, глубокоматовая, подготовка Q3	Tikkurila F485 «Damask»	13,6 м²
О7	акцентная стена	окраска, Tikkurila Euro Power 7, колеровка по NCS, матовая, подготовка Q3	NCS S 5010-G70Y «S 5010-G70Y»	6,3 м²

Примечания

1. Размеры — в мм от чистовых поверхностей стен; условные обозначения и общие указания — лист 2.
2. Карнизы (шины) — по ведомости текстиля декоратора; длина L и верх H — по развёртке, крепление — до окраски потолка.
3. Потолок на развёртках — по нижнему уровню У1; другие уровни потолка помещения: У2 +2,600.

					Проект: Квартира 56 м²
	Лист	№ док.	Подпись	Дата	Развёртка стены А. Спальня (пом. 2)
Дизайнер	Кырлан А.С.			19.10.26	

Стадия	Лист	Листов
П	35	56

выпуск 19.10.2026 № 60226ce68e · стр. 35 из 56

Развёртка стены Б


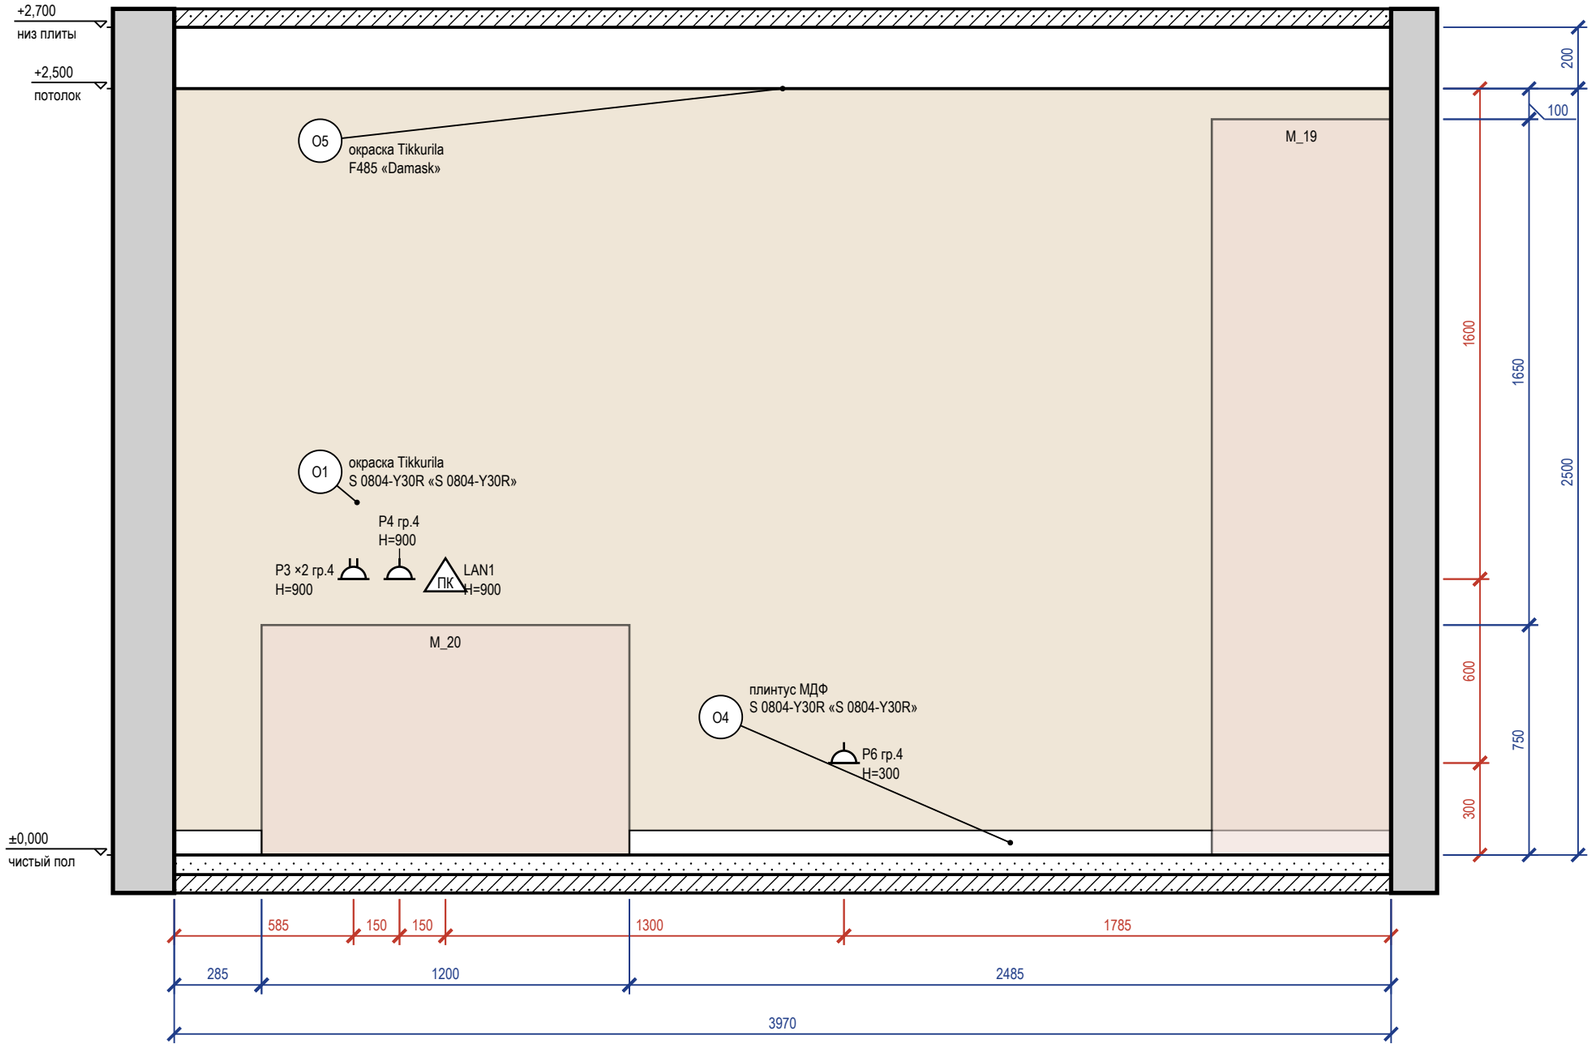


Схема развёрток (М 1:100)

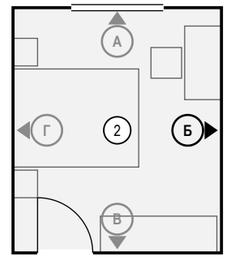

Ведомость отделки (на листе)

Марка	Поверхность	Материал, изделие	Цвет, код	Кол.
О1	стены	окраска, Tikkurila Euro Power 7, колеровка по NCS, матовая, подготовка Q3	NCS S 0804-Y30R «S 0804-Y30R»	9,9 м²
О4	плинтус	плинтус МДФ, h 80 мм, аналог: плинтус МДФ под покраску 80×16	NCS S 0804-Y30R «S 0804-Y30R»	2,8 м
О5	потолок	окраска, Tikkurila Euro Power 7, глубокоматовая, подготовка Q3	Tikkurila F485 «Damask»	13,6 м²

Примечания

1. Размеры — в мм от чистовых поверхностей стен; условные обозначения и общие указания — лист 2.
2. Потолок на развёртках — по нижнему уровню У1; другие уровни потолка помещения: У2 +2,600.

	Лист	№ док.	Подпись	Дата
Дизайнер	Кырлан А.С.			19.10.26

Проект: Квартира 56 м²

Развёртка стены Б. Спальня (пом. 2)

Стадия	Лист	Листов
П	36	56

выпуск 19.10.2026 № 60226ce68e · стр. 36 из 56

Развёртка стены В


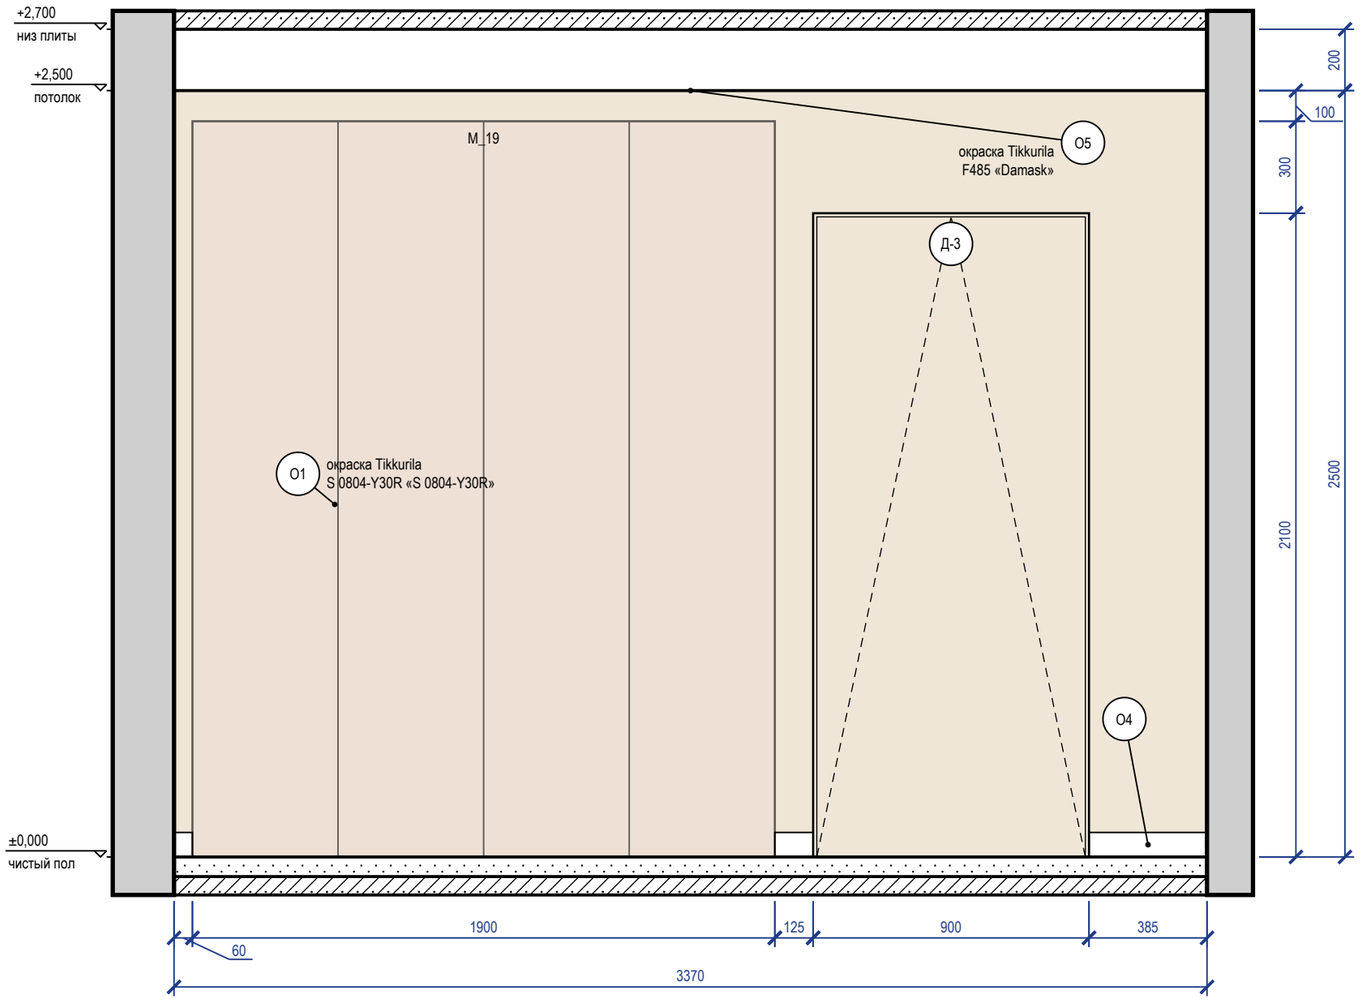


Схема развёрток (М 1:100)

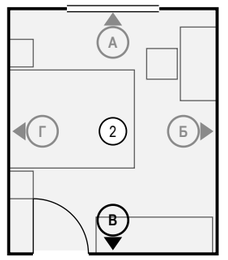


Ведомость отделки (на листе)

Марка	Поверхность	Материал, изделие	Цвет, код	Кол.
О1	стены	окраска, Tikkurila Euro Power 7, колеровка по NCS, матовая, подготовка Q3	NCS S 0804-Y30R «S 0804-Y30R»	6,5 м²
О4	плинтус	плинтус МДФ, h 80 мм, аналог: плинтус МДФ под покраску 80×16	NCS S 0804-Y30R «S 0804-Y30R»	0,6 м
О5	потолок	окраска, Tikkurila Euro Power 7, глубокоматовая, подготовка Q3	Tikkurila F485 «Damask»	13,6 м²

6 **Плинтус МДФ 80×16 мм у окрашенной стены (М 1:10)**

Узел 6 — лист С3

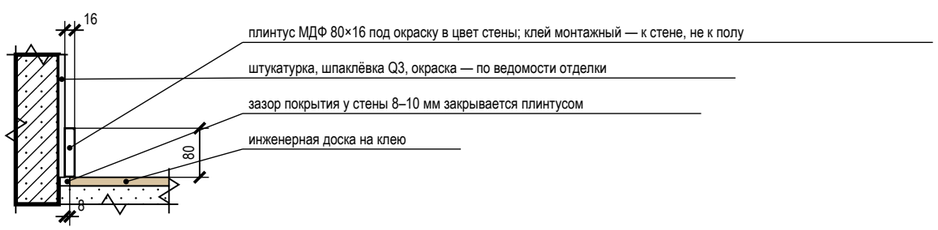

Примечания

1. Размеры — в мм от чистовых поверхностей стен; условные обозначения и общие указания — лист 2.
2. Двери скрытого монтажа — полотно в плоскости стены, отделка стены по полотну, плинтус прерывается у короба (узел — на листе узлов).
3. Потолок на развёртках — по нижнему уровню У1; другие уровни потолка помещения: У2 +2,600.

					Проект: Квартира 56 м²
	Лист	№ док.	Подпись	Дата	Развёртка стены В. Спальня (пом. 2)
Дизайнер	Кырлан А.С.			19.10.26	

Стадия	Лист	Листов
П	37	56

выпуск 19.10.2026 № 60226ce68e · стр. 37 из 56

Развёртка стены Г


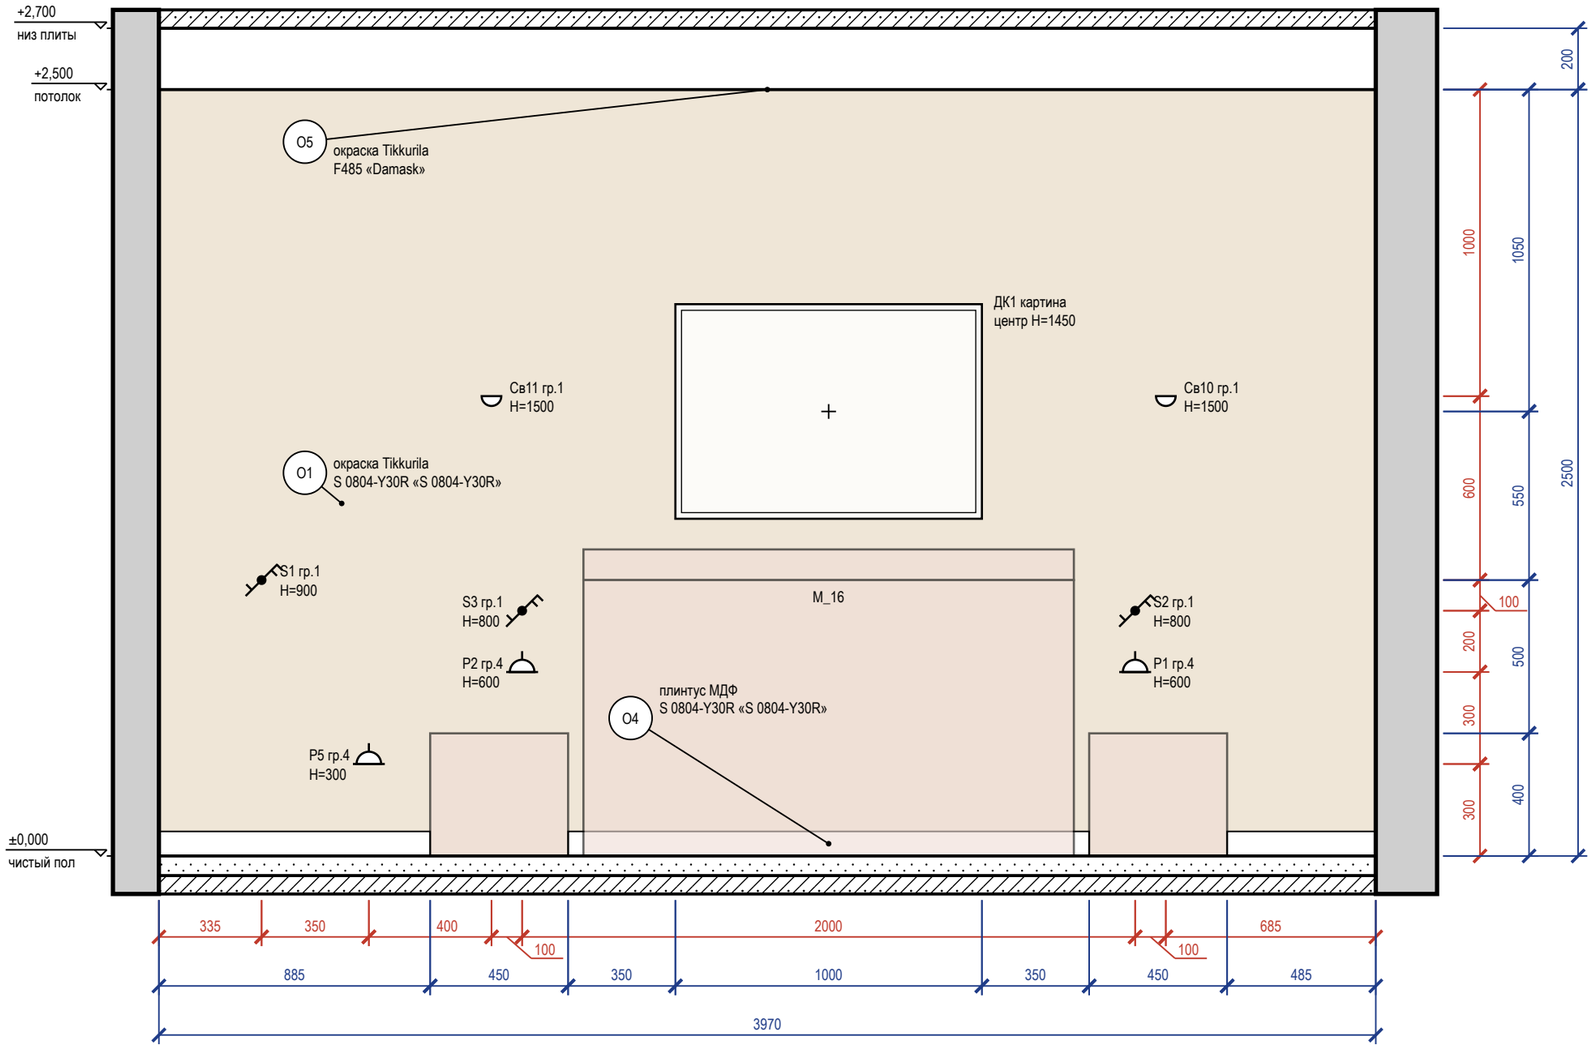


Схема развёрток (М 1:100)

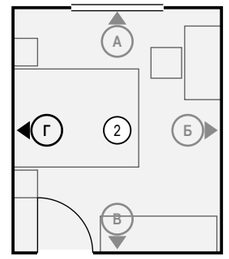

Ведомость отделки (на листе)

Марка	Поверхность	Материал, изделие	Цвет, код	Кол.
О1	стены	окраска, Tikkurila Euro Power 7, колеровка по NCS, матовая, подготовка Q3	NCS S 0804-Y30R «S 0804-Y30R»	9,9 м²
О4	плинтус	плинтус МДФ, h 80 мм, аналог: плинтус МДФ под покраску 80×16	NCS S 0804-Y30R «S 0804-Y30R»	3,1 м
О5	потолок	окраска, Tikkurila Euro Power 7, глубокоматовая, подготовка Q3	Tikkurila F485 «Damask»	13,6 м²

Примечания

1. Размеры — в мм от чистовых поверхностей стен; условные обозначения и общие указания — лист 2.
2. Картины и зеркала крепить к основанию по паспорту изделия (закладные и анкеры — в перечне скрытых работ); крест — ось центра предмета.
3. Потолок на развёртках — по нижнему уровню У1; другие уровни потолка помещения: У2 +2,600.

					Проект: Квартира 56 м²
	Лист	№ док.	Подпись	Дата	
Дизайнер	Кырлан А.С.			19.10.26	Развёртка стены Г. Спальня (пом. 2)

Стадия	Лист	Листов
П	38	56

выпуск 19.10.2026 № 60226ce68e · стр. 38 из 56

Развёртка стены А


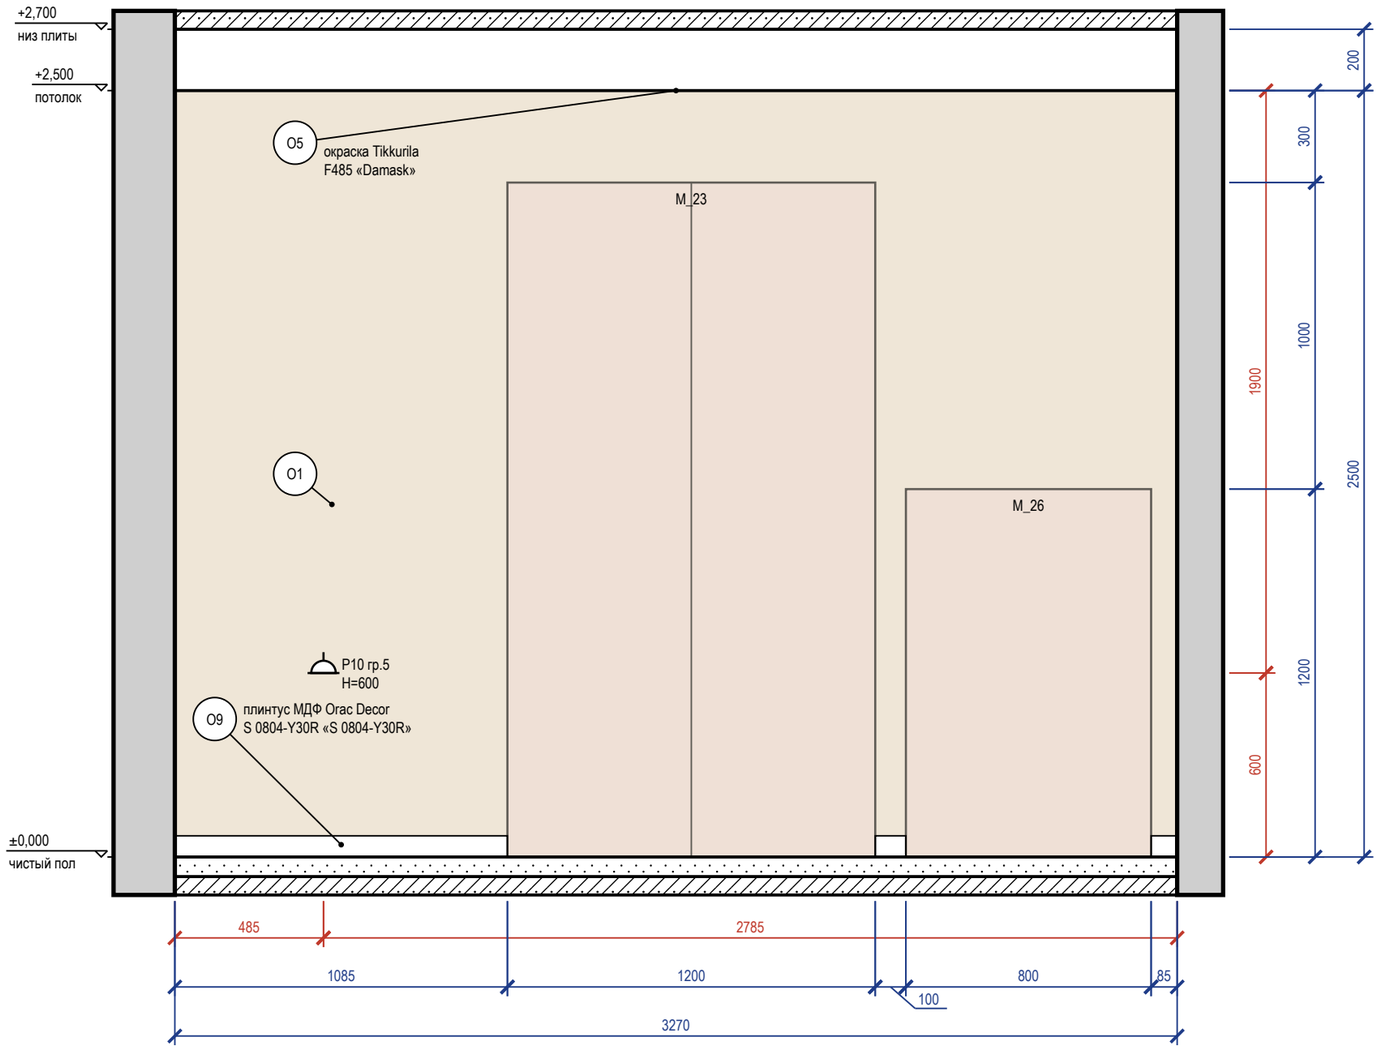


Схема развёрток (М 1:100)

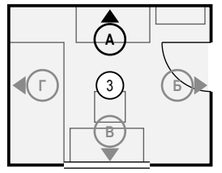

Ведомость отделки (на листе)

Марка	Поверхность	Материал, изделие	Цвет, код	Кол.
О1	стены	окраска, Tikkurila Euro Power 7, колеровка по NCS, матовая, подготовка Q3	NCS S 0804-Y30R «S 0804-Y30R»	8,2 м²
О5	потолок	окраска, Tikkurila Euro Power 7, глубокоматовая, подготовка Q3	Tikkurila F485 «Damask»	8,6 м²
О9	плинтус	плинтус МДФ, Orac Decor Contour (Luxxus), h 69 мм, SX165	NCS S 0804-Y30R «S 0804-Y30R»	1,3 м

Примечания

1. Размеры — в мм от чистовых поверхностей стен; условные обозначения и общие указания — лист 2.
2. Потолок на развёртках — по нижнему уровню У1; другие уровни потолка помещения: У2 +2,600.

					Проект: Квартира 56 м²
	Лист	№ док.	Подпись	Дата	Развёртка стены А. Детская (пом. 3)
Дизайнер	Кырлан А.С.			19.10.26	

Стадия	Лист	Листов
П	39	56

выпуск 19.10.2026 № 60226ce68e · стр. 39 из 56

Развёртка стены Б


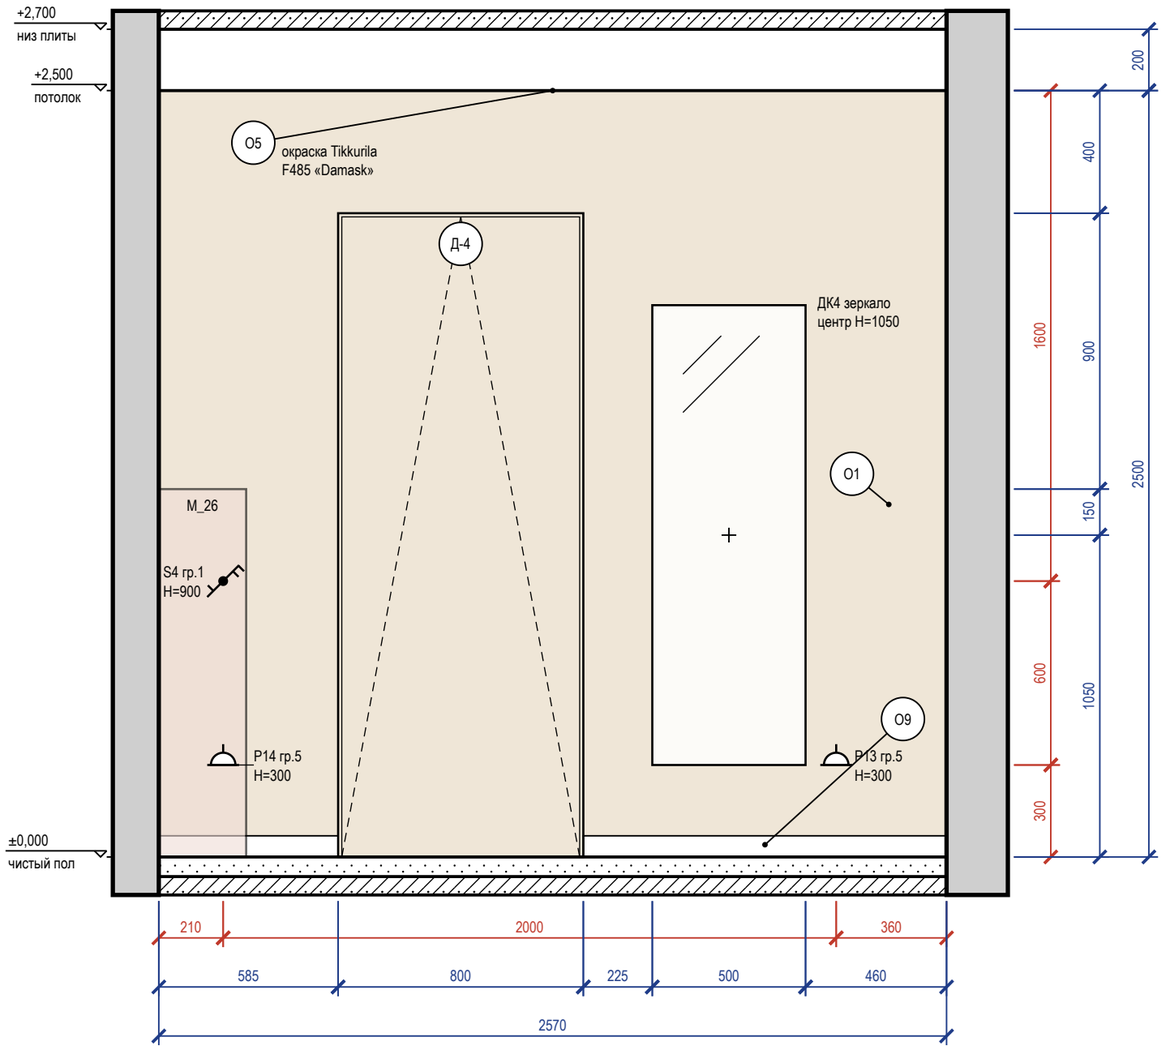


Схема развёрток (М 1:100)

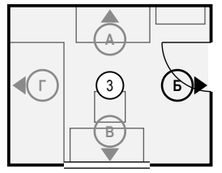

Ведомость отделки (на листе)

Марка	Поверхность	Материал, изделие	Цвет, код	Кол.
О1	стены	окраска, Tikkurila Euro Power 7, колеровка по NCS, матовая, подготовка Q3	NCS S 0804-Y30R «S 0804-Y30R»	4,7 м²
О5	потолок	окраска, Tikkurila Euro Power 7, глубокоматовая, подготовка Q3	Tikkurila F485 «Damask»	8,6 м²
О9	плинтус	плинтус МДФ, Orac Decor Contour (Luxxus), h 69 мм, SX165	NCS S 0804-Y30R «S 0804-Y30R»	1,8 м

Примечания

1. Размеры — в мм от чистовых поверхностей стен; условные обозначения и общие указания — лист 2.
2. Картины и зеркала крепить к основанию по паспорту изделия (закладные и анкеры — в перечне скрытых работ); крест — ось центра предмета.
3. Двери скрытого монтажа — полотно в плоскости стены, отделка стены по полотну, плинтус прерывается у короба (узел — на листе узлов).
4. Потолок на развёртках — по нижнему уровню У1; другие уровни потолка помещения: У2 +2,600.

					Проект: Квартира 56 м²
	Лист	№ док.	Подпись	Дата	Развёртка стены Б. Детская (пом. 3)
Дизайнер	Кырлан А.С.			19.10.26	

Стадия	Лист	Листов
П	40	56

выпуск 19.10.2026 № 60226ce68e · стр. 40 из 56

Развёртка стены В


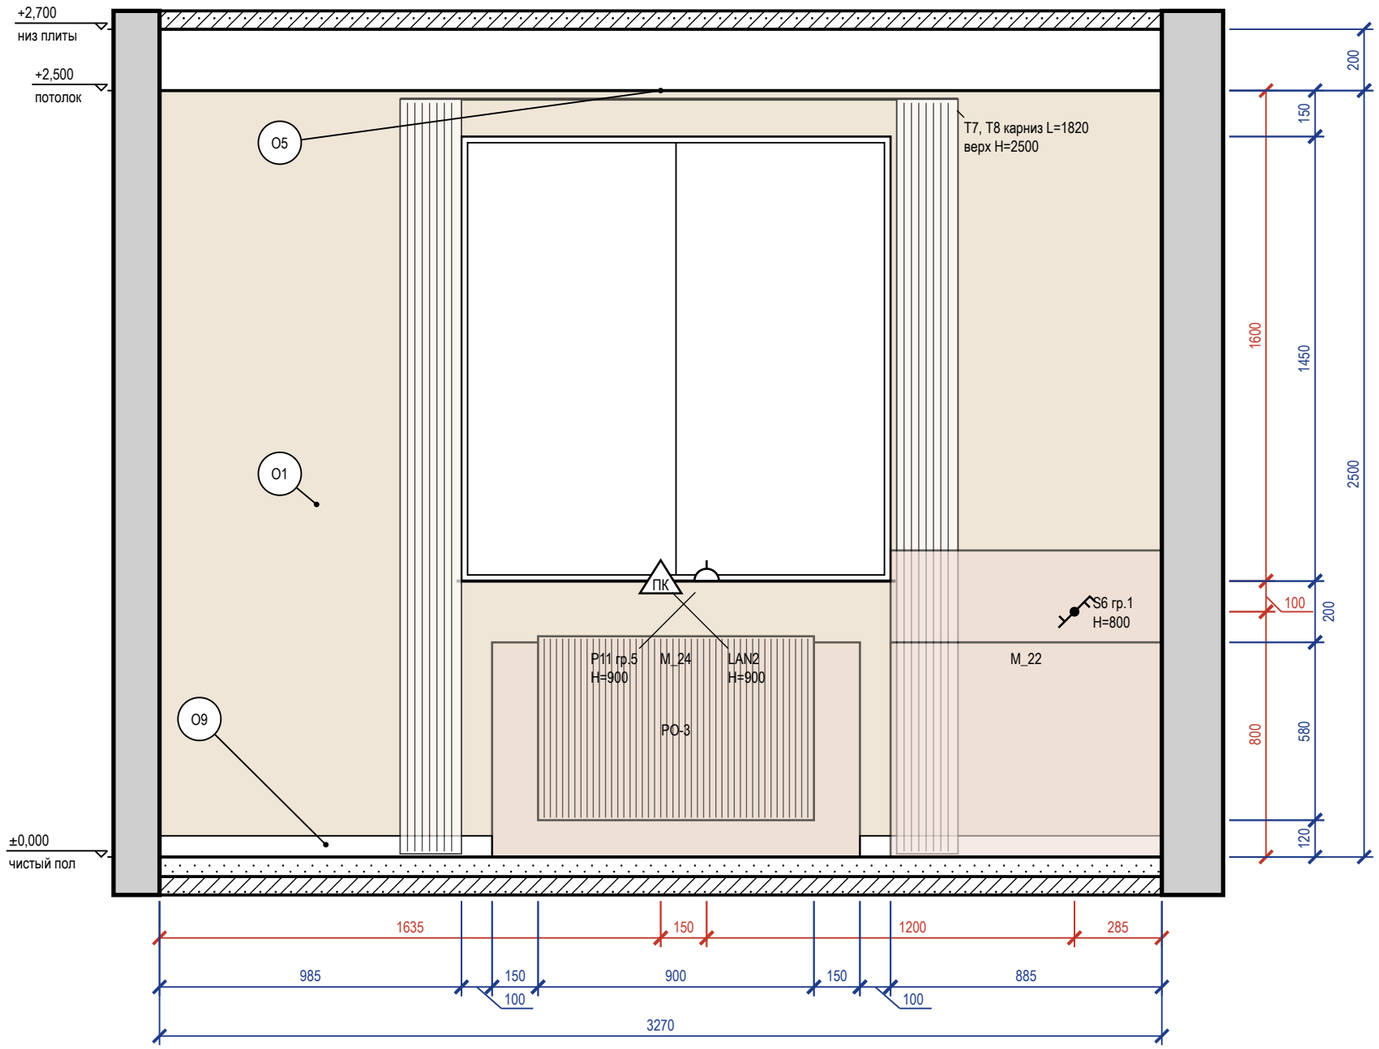


Схема развёрток (М 1:100)

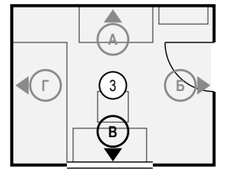

Ведомость отделки (на листе)

Марка	Поверхность	Материал, изделие	Цвет, код	Кол.
О1	стены	окраска, Tikkurila Euro Power 7, колеровка по NCS, матовая, подготовка Q3	NCS S 0804-Y30R «S 0804-Y30R»	6,1 м²
О5	потолок	окраска, Tikkurila Euro Power 7, глубокоматовая, подготовка Q3	Tikkurila F485 «Damask»	8,6 м²
О9	плинтус	плинтус МДФ, Orac Decor Contour (Luxxus), h 69 мм, SX165	NCS S 0804-Y30R «S 0804-Y30R»	2,1 м

Примечания

1. Размеры — в мм от чистовых поверхностей стен; условные обозначения и общие указания — лист 2.
2. Карнизы (шины) — по ведомости текстиля декоратора; длина L и верх H — по развёртке, крепление — до окраски потолка.
3. Потолок на развёртках — по нижнему уровню У1; другие уровни потолка помещения: У2 +2,600.

					Проект: Квартира 56 м²
	Лист	№ док.	Подпись	Дата	Развёртка стены В. Детская (пом. 3)
Дизайнер	Кырлан А.С.			19.10.26	

Стадия	Лист	Листов
П	41	56

выпуск 19.10.2026 № 60226ce68e · стр. 41 из 56

Развёртка стены Г


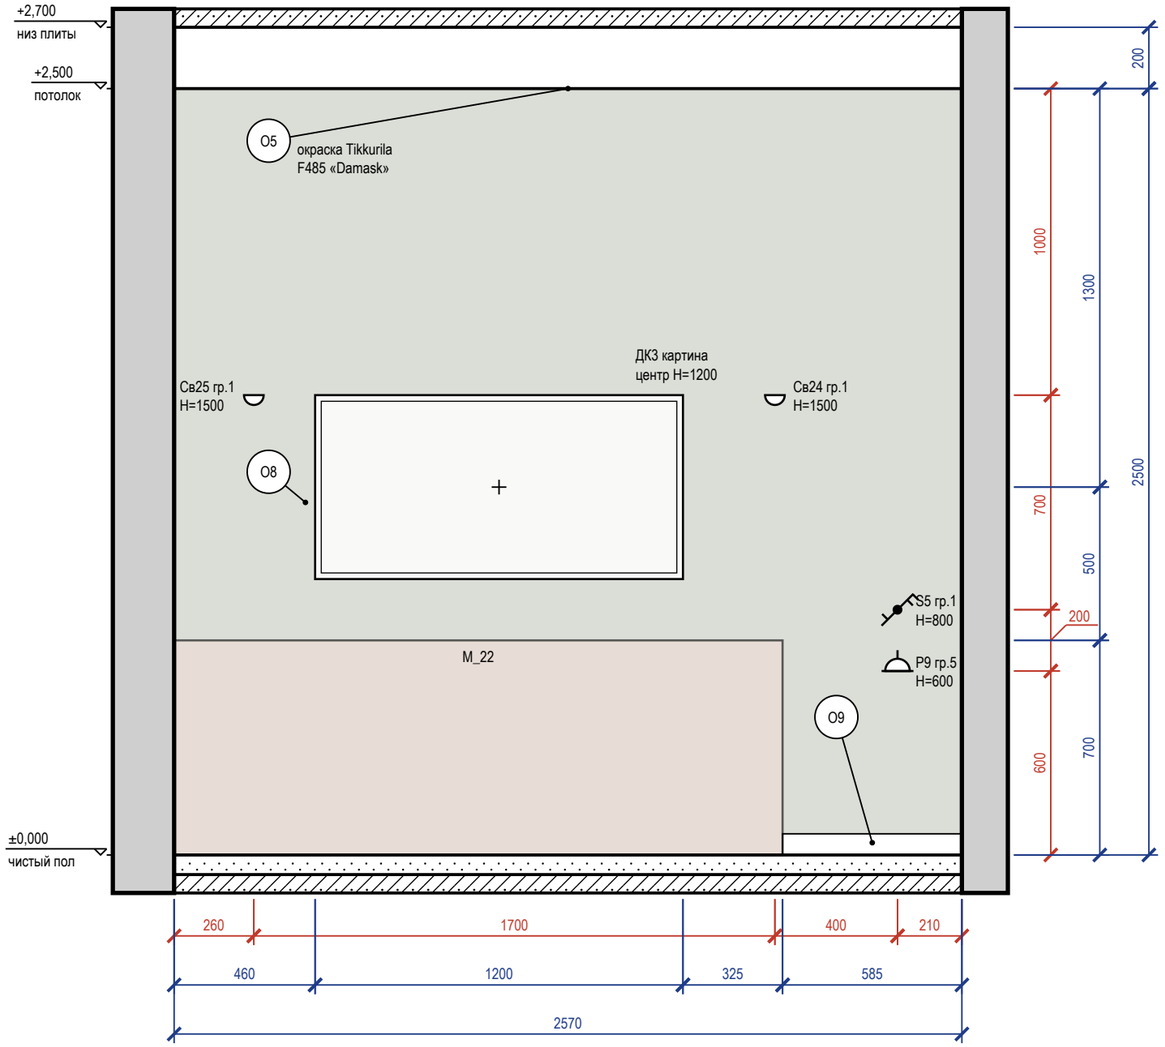


Схема развёрток (М 1:100)

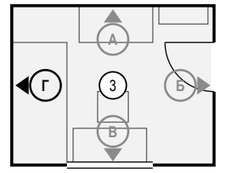

Ведомость отделки (на листе)

Марка	Поверхность	Материал, изделие	Цвет, код	Кол.
О5	потолок	окраска, Tikkurila Euro Power 7, глубокоматовая, подготовка Q3	Tikkurila F485 «Damask»	8,6 м²
О8	акцентная стена	окраска, Tikkurila Euro Power 7, матовая, подготовка Q3	Tikkurila X447 «Sea Smoke»	6,4 м²
О9	плинтус	плинтус МДФ, Orac Decor Contour (Luxxus), h 69 мм, SX165	NCS S 0804-Y30R «S 0804-Y30R»	0,6 м

Примечания

1. Размеры — в мм от чистовых поверхностей стен; условные обозначения и общие указания — лист 2.
2. Картины и зеркала крепить к основанию по паспорту изделия (закладные и анкеры — в перечне скрытых работ); крест — ось центра предмета.
3. Потолок на развёртках — по нижнему уровню У1; другие уровни потолка помещения: У2 +2,600.

	Лист	№ док.	Подпись	Дата
Дизайнер	Кырлан А.С.			19.10.26


Проект: Квартира 56 м²

Развёртка стены Г. Детская (пом. 3)

Стадия	Лист	Листов
П	42	56

выпуск 19.10.2026 № 60226ce68e · стр. 42 из 56

Развёртка стены А

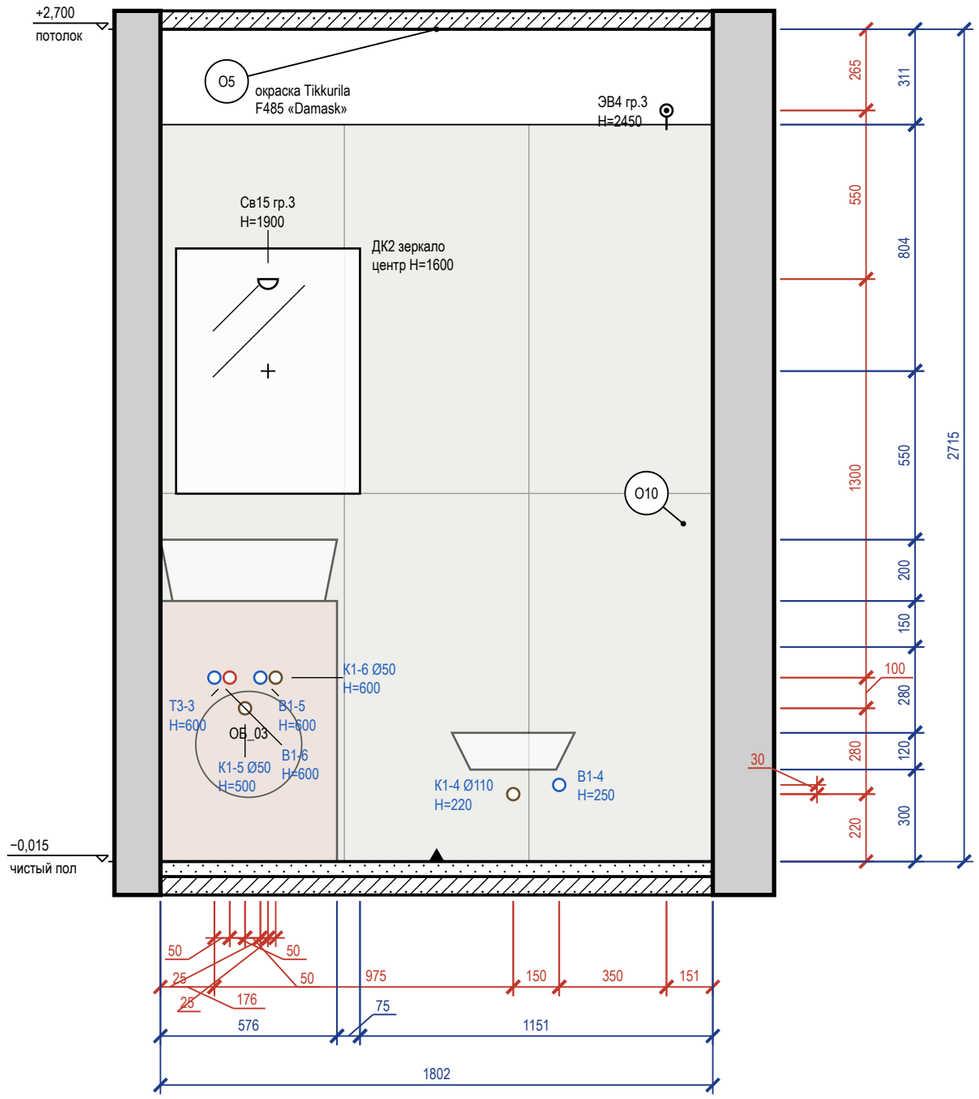

Развёртка стены Б


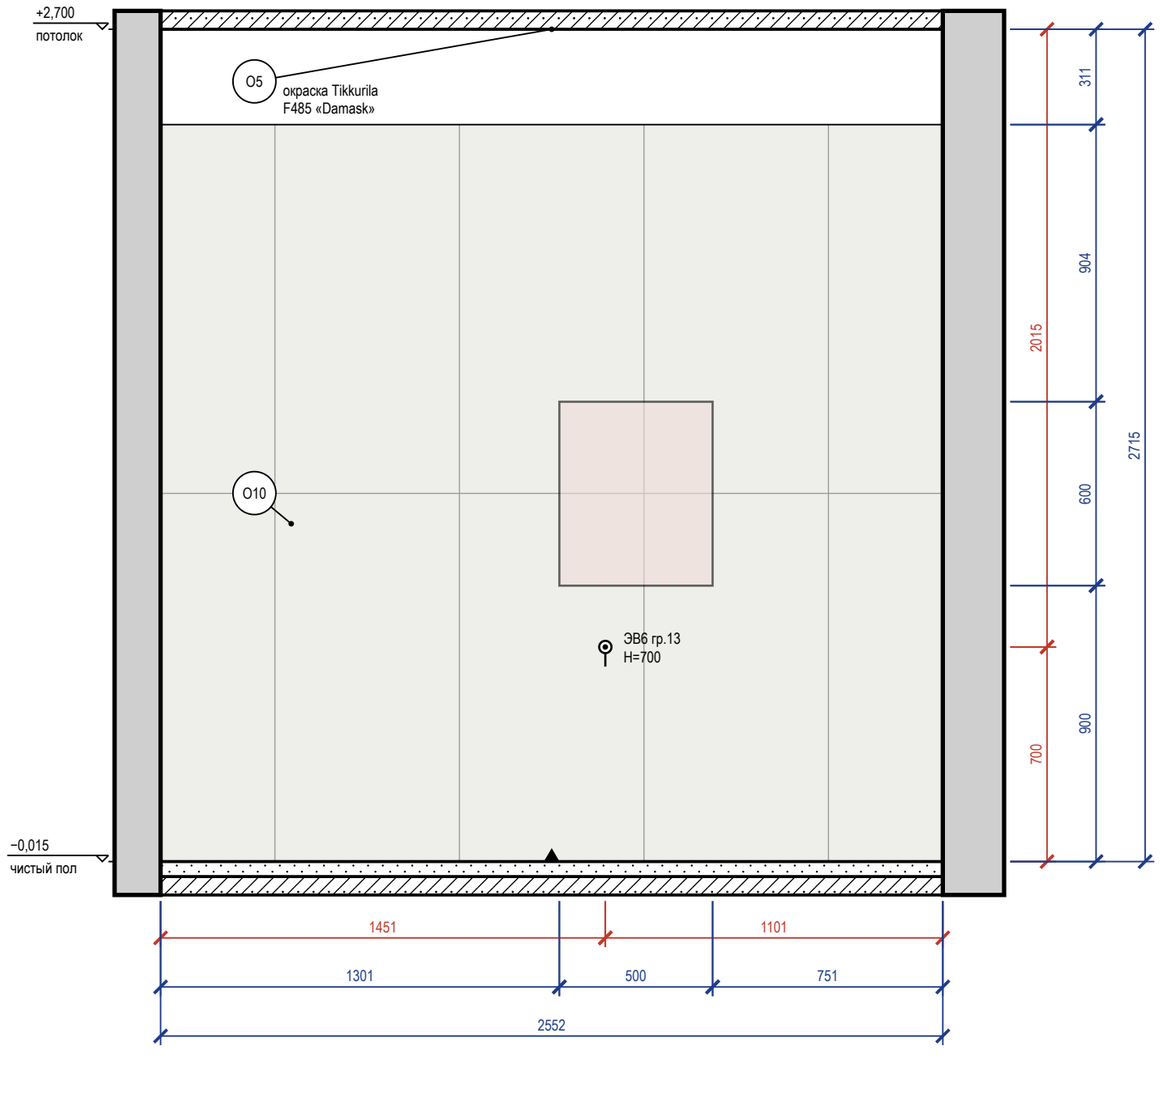


Схема развёрток (М 1:100)

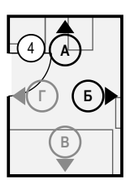

Ведомость отделки (на листе)

Марка	Поверхность	Материал, изделие	Цвет, код	Кол.
О5	потолок	окраска, Tikkurila Euro Power 7, матовая, подготовка Q3	Tikkurila F485 «Damask»	4,8 м²
О10	стены	облицовка плиткой, Atlas Concorde Marvel Travertine, 600×1200×9 мм, A8UZ, затирка CG2WA	Atlas Concorde A8UZ «Marvel Travertine»	10,5 м²

Примечания


1. Размеры — в мм от чистовых поверхностей стен; условные обозначения и общие указания — лист 2.
2. Схема мебели, приборов и декора не является технической документацией для производства мебели; габариты — по паспортам изделий.
3. Выводы ВК — коды и высоты по листу выводов сантехники.
4. Облицовка — по сетке швов 2 мм, раскладка от оси стены (треугольник у пола), целые ряды от пола; подрезки — по листу раскладки плитки.
5. Гидроизоляция в 2 слоя, заход на стены 200 мм — до облицовки, с актом скрытых работ и тестом проливом (узел — на листе узлов).
6. Картины и зеркала крепить к основанию по паспорту изделия (закладные и анкеры — в перечне скрытых работ); крест — ось центра предмета.

					Проект: Квартира 56 м²
	Лист	№ док.	Подпись	Дата	Развёртки стен А, Б. Санузел (пом. 4)
Дизайнер	Кырлан А.С.			19.10.26	

Стадия	Лист	Листов
П	43	56

выпуск 19.10.2026 № 60226ce68e · стр. 43 из 56

Развёртка стены В

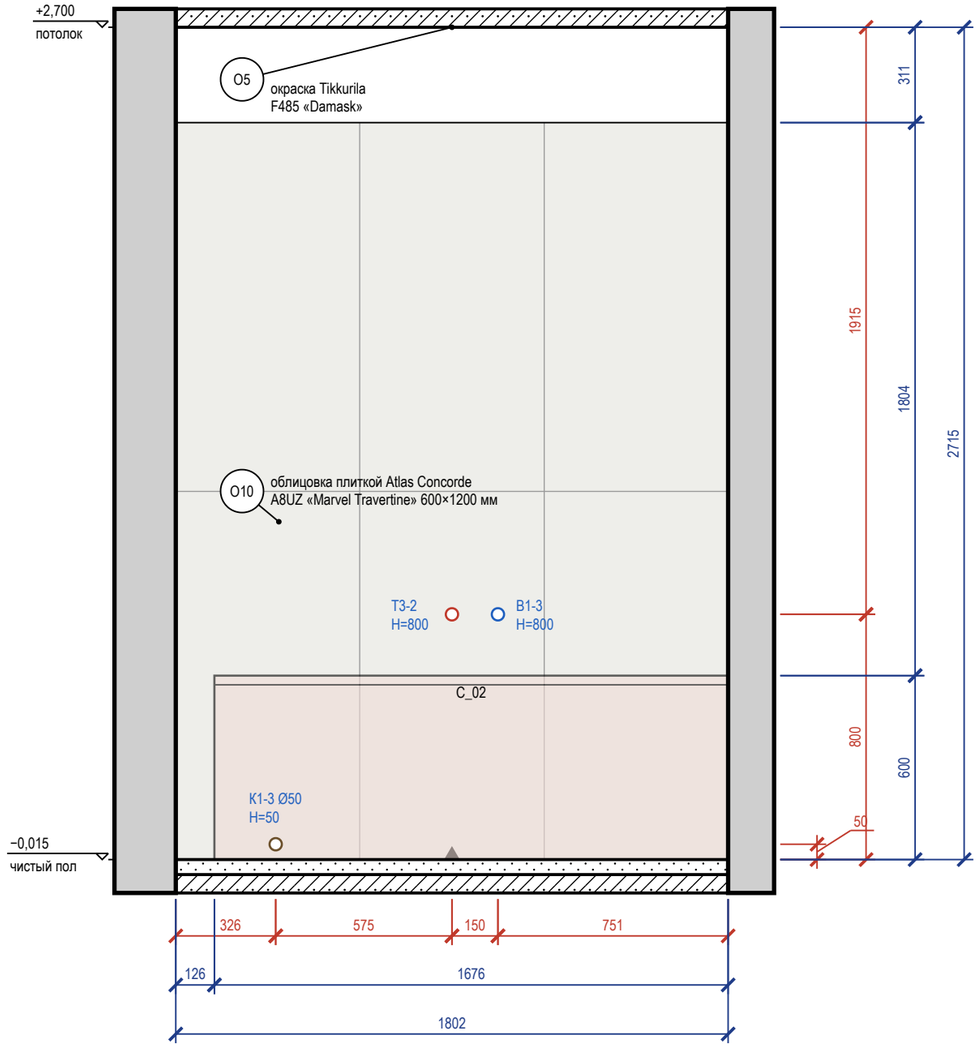

Развёртка стены Г


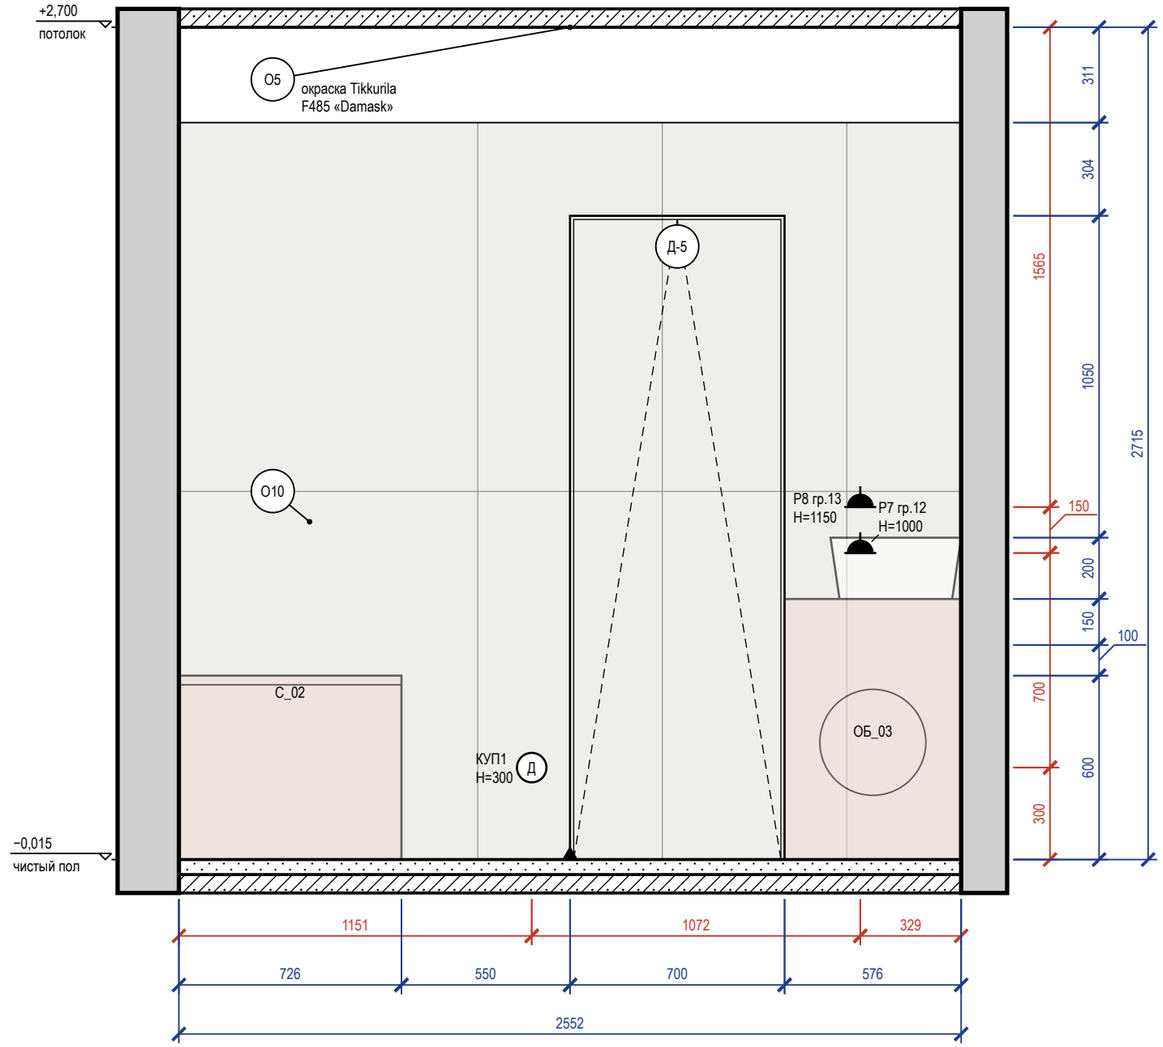


Схема развёрток (М 1:100)

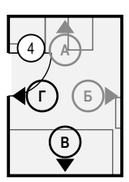

Ведомость отделки (на листе)

Марка	Поверхность	Материал, изделие	Цвет, код	Кол.
О5	потолок	окраска, Tikkurila Euro Power 7, матовая, подготовка Q3	Tikkurila F485 «Damask»	4,8 м²
О10	стены	облицовка плиткой, Atlas Concorde Marvel Travertine, 600×1200×9 мм, A8UZ, затирка CG2WA	Atlas Concorde A8UZ «Marvel Travertine»	9 м²

Примечания

1. Размеры — в мм от чистовых поверхностей стен; условные обозначения и общие указания — лист 2.
2. Схема мебели, приборов и декора не является технической документацией для производства мебели; габариты — по паспортам изделий.
3. Выводы ВК — коды и высоты по листу выводов сантехники.
4. Облицовка — по сетке швов 2 мм, раскладка от оси стены (треугольник у пола), целые ряды от пола; подрезки — по листу раскладки плитки.
5. Гидроизоляция в 2 слоя, заход на стены 200 мм — до облицовки, с актом скрытых работ и тестом проливом (узел — на листе узлов).
6. Двери скрытого монтажа — полотно в плоскости стены, отделка стены по полотну, плинтус прерывается у короба (узел — на листе узлов).

					Проект: Квартира 56 м²
	Лист	№ док.	Подпись	Дата	Развёртки стен В, Г. Санузел (пом. 4)
Дизайнер	Кырлан А.С.			19.10.26	

Стадия	Лист	Листов
П	44	56

выпуск 19.10.2026 № 60226ce68e · стр. 44 из 56

Развёртка стены А


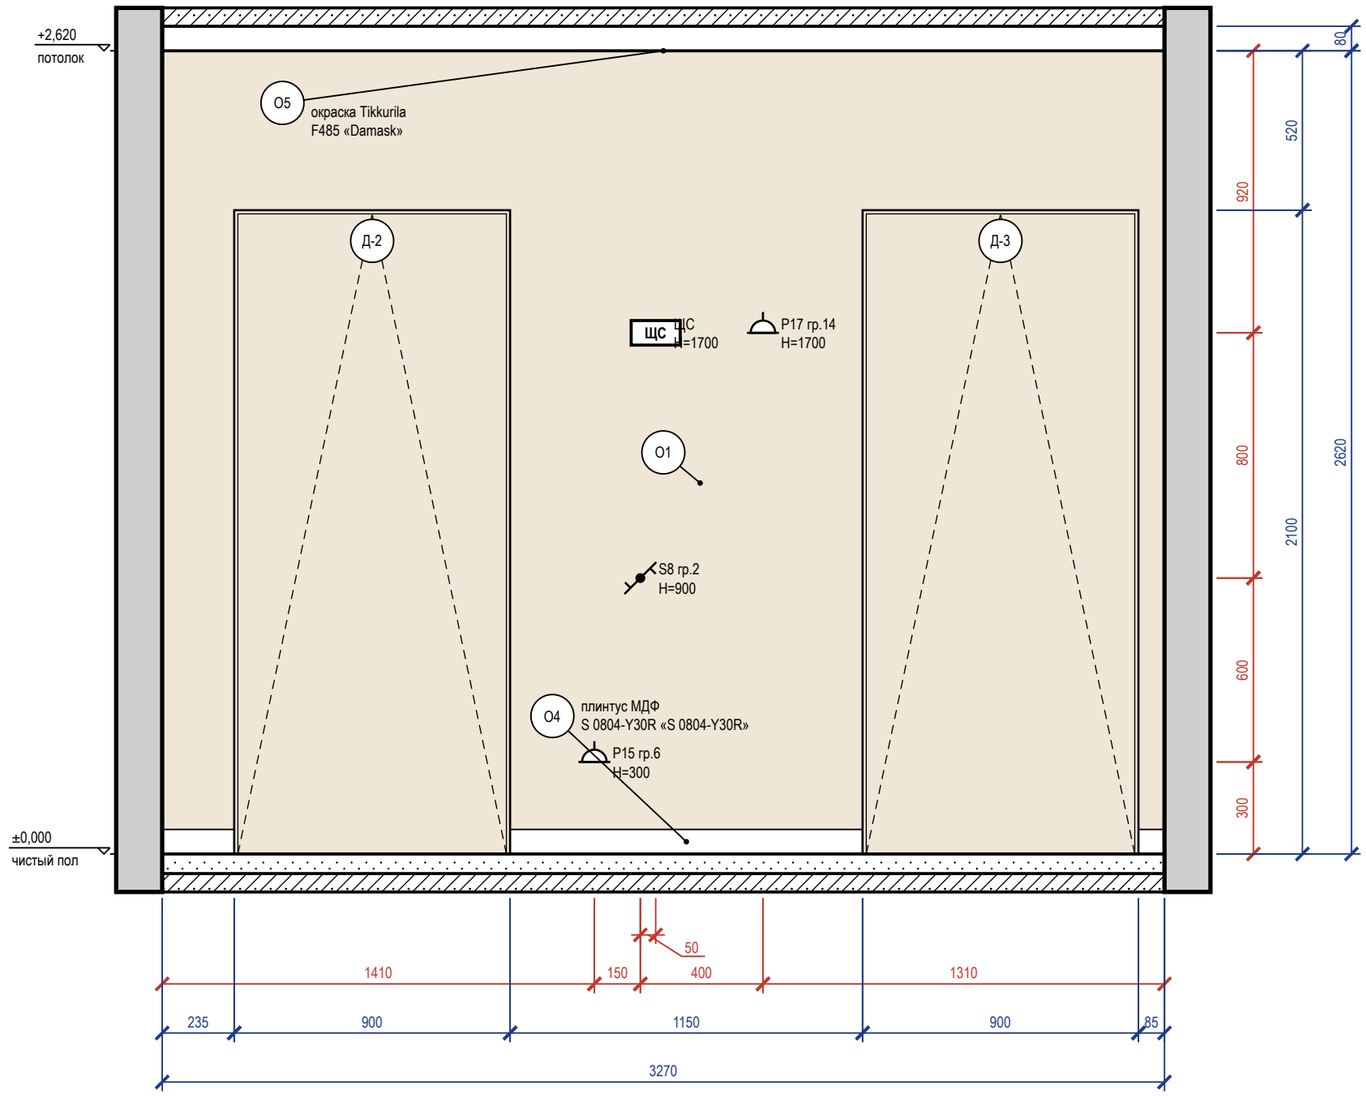


Схема развёрток (М 1:100)

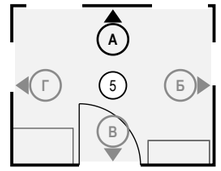

Ведомость отделки (на листе)

Марка	Поверхность	Материал, изделие	Цвет, код	Кол.
О1	стены	окраска, Tikkurila Euro Power 7, колеровка по NCS, матовая, подготовка Q3	NCS S 0804-Y30R «S 0804-Y30R»	4,8 м²
О4	плинтус	плинтус МДФ, h 80 мм, аналог: плинтус МДФ под покраску 80×16	NCS S 0804-Y30R «S 0804-Y30R»	1,5 м
О5	потолок	окраска, Tikkurila Euro Power 7, глубокоматовая, подготовка Q3	Tikkurila F485 «Damask»	8,6 м²

Примечания

1. Размеры — в мм от чистовых поверхностей стен; условные обозначения и общие указания — лист 2.
2. Двери скрытого монтажа — полотно в плоскости стены, отделка стены по полотну, плинтус прерывается у короба (узел — на листе узлов).

					Проект: Квартира 56 м²
	Лист	№ док.	Подпись	Дата	Развёртка стены А. Прихожая (пом. 5)
Дизайнер	Кырлан А.С.			19.10.26	

Стадия	Лист	Листов
П	45	56

выпуск 19.10.2026 № 60226ce68e · стр. 45 из 56

Развёртка стены Б


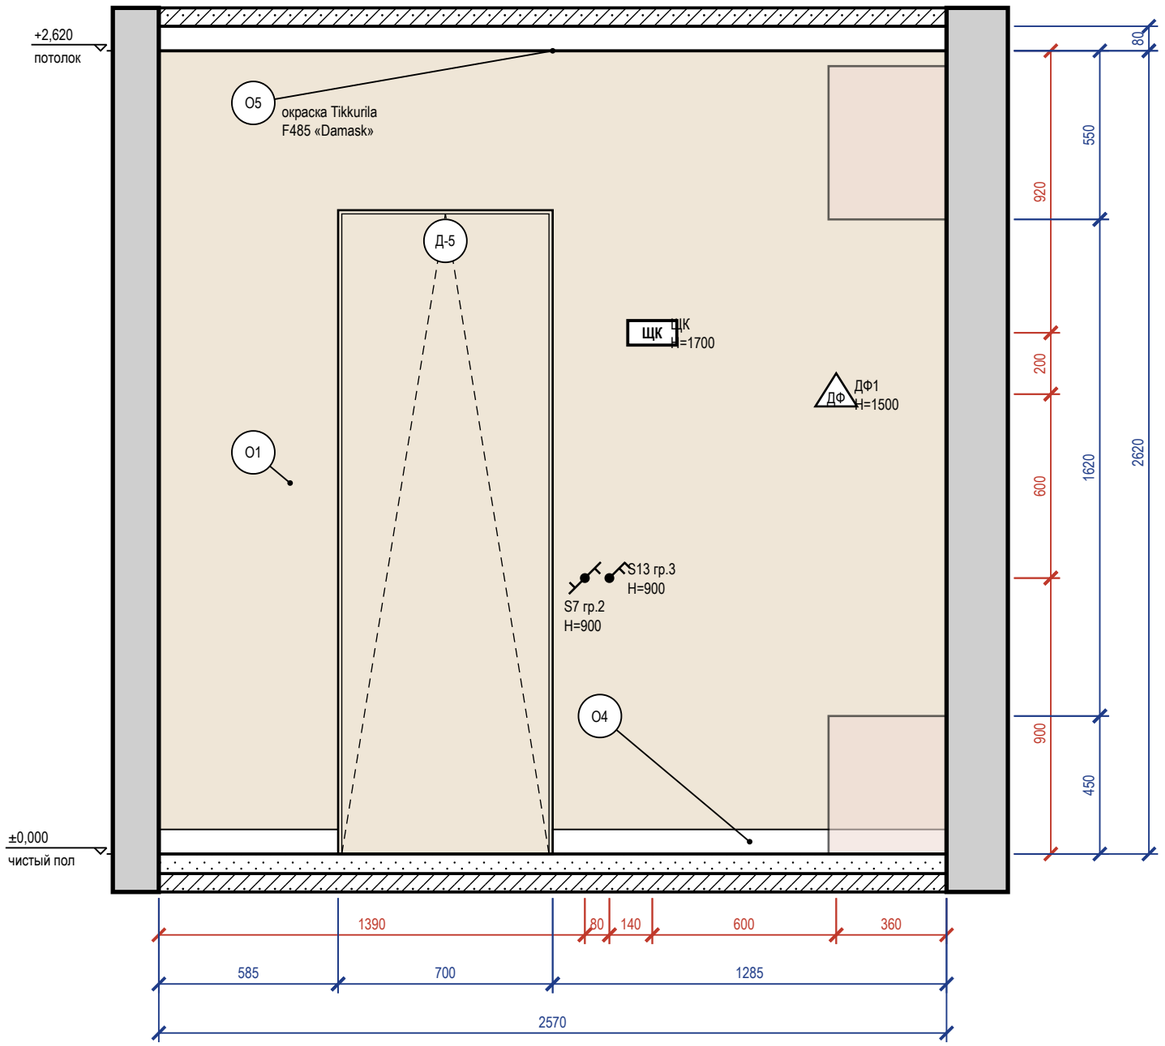


Схема развёрток (М 1:100)

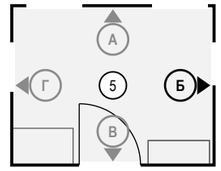

Ведомость отделки (на листе)

Марка	Поверхность	Материал, изделие	Цвет, код	Кол.
О1	стены	окраска, Tikkurila Euro Power 7, колеровка по NCS, матовая, подготовка Q3	NCS S 0804-Y30R «S 0804-Y30R»	5,3 м²
О4	плинтус	плинтус МДФ, h 80 мм, аналог: плинтус МДФ под покраску 80×16	NCS S 0804-Y30R «S 0804-Y30R»	1,9 м
О5	потолок	окраска, Tikkurila Euro Power 7, глубокоматовая, подготовка Q3	Tikkurila F485 «Damask»	8,6 м²

Примечания

1. Размеры — в мм от чистовых поверхностей стен; условные обозначения и общие указания — лист 2.
2. Двери скрытого монтажа — полотно в плоскости стены, отделка стены по полотну, плинтус прерывается у короба (узел — на листе узлов).

					Проект: Квартира 56 м²
	Лист	№ док.	Подпись	Дата	Развёртка стены Б. Прихожая (пом. 5)
Дизайнер	Кырлан А.С.			19.10.26	

Стадия	Лист	Листов
П	46	56

выпуск 19.10.2026 № 60226ce68e · стр. 46 из 56

Развёртка стены В


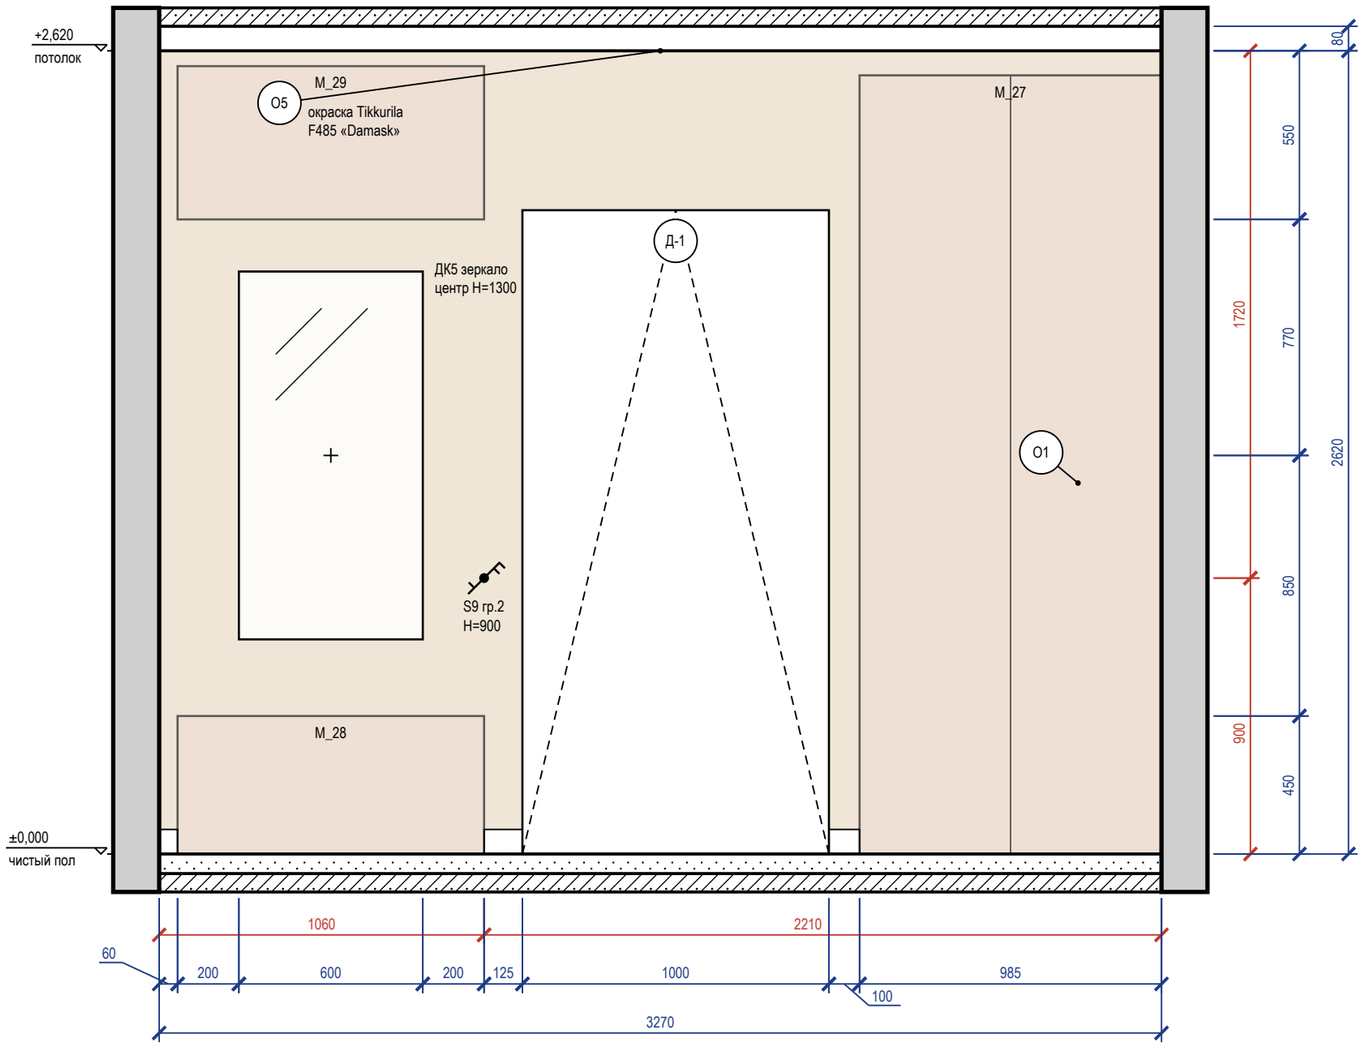


Схема развёрток (М 1:100)

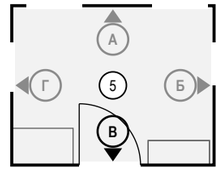

Ведомость отделки (на листе)

Марка	Поверхность	Материал, изделие	Цвет, код	Кол.
О1	стены	окраска, Tikkurila Euro Power 7, колеровка по NCS, матовая, подготовка Q3	NCS S 0804-Y30R «S 0804-Y30R»	6,5 м²
О4	плинтус	плинтус МДФ, h 80 мм, аналог: плинтус МДФ под покраску 80×16	NCS S 0804-Y30R «S 0804-Y30R»	0,3 м
О5	потолок	окраска, Tikkurila Euro Power 7, глубокоматовая, подготовка Q3	Tikkurila F485 «Damask»	8,6 м²

Примечания

1. Размеры — в мм от чистовых поверхностей стен; условные обозначения и общие указания — лист 2.
2. Картины и зеркала крепить к основанию по паспорту изделия (закладные и анкеры — в перечне скрытых работ); крест — ось центра предмета.

					Проект: Квартира 56 м²
	Лист	№ док.	Подпись	Дата	Развёртка стены В. Прихожая (пом. 5)
Дизайнер	Кырлан А.С.			19.10.26	

Стадия	Лист	Листов
П	47	56

выпуск 19.10.2026 № 60226ce68e · стр. 47 из 56

Развёртка стены Г


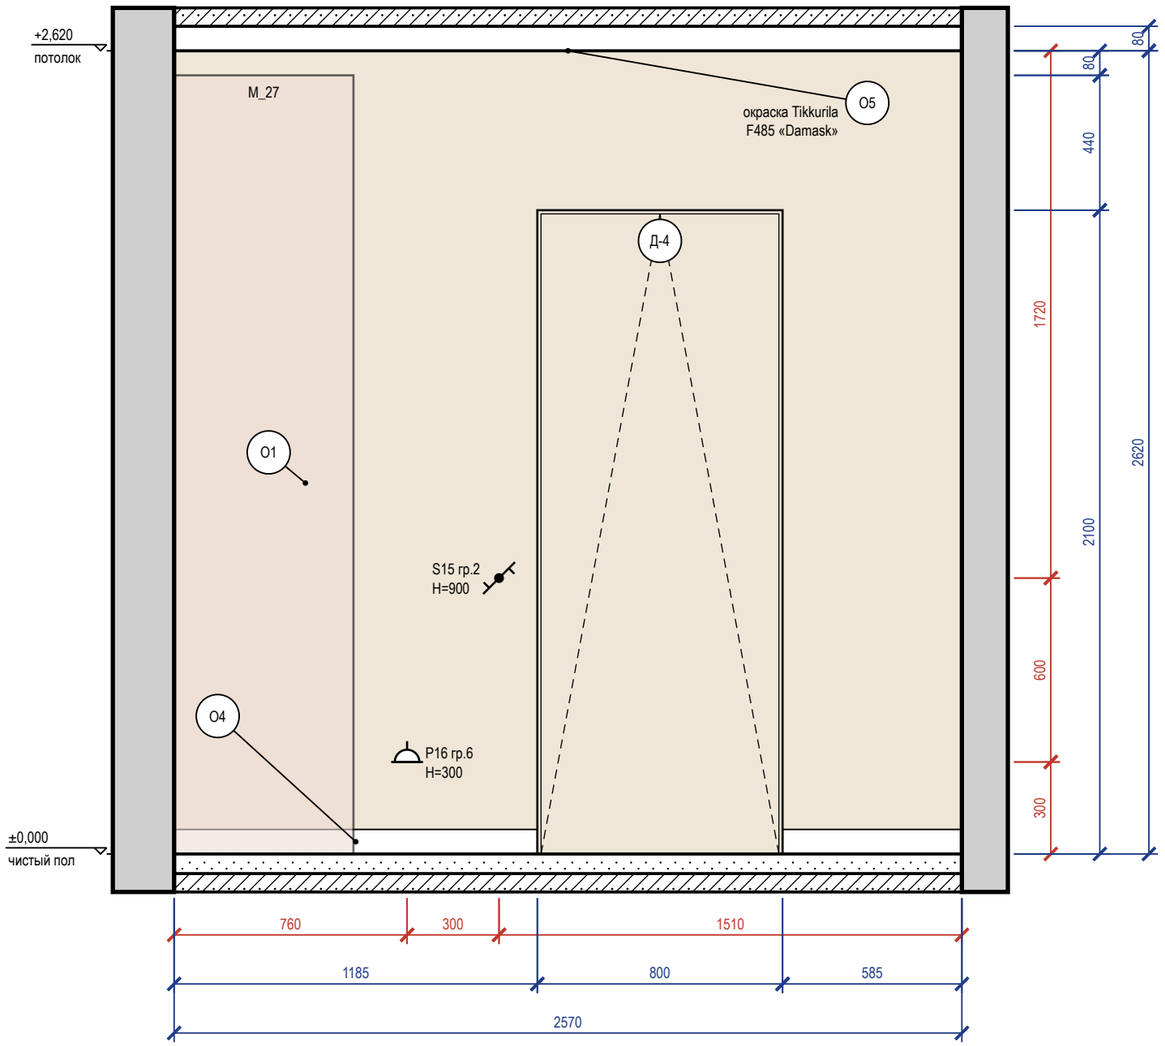


Схема развёрток (М 1:100)

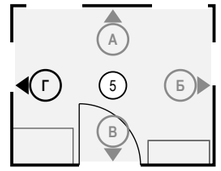

Ведомость отделки (на листе)

Марка	Поверхность	Материал, изделие	Цвет, код	Кол.
О1	стены	окраска, Tikkurila Euro Power 7, колеровка по NCS, матовая, подготовка Q3	NCS S 0804-Y30R «S 0804-Y30R»	5,1 м²
О4	плинтус	плинтус МДФ, h 80 мм, аналог: плинтус МДФ под покраску 80×16	NCS S 0804-Y30R «S 0804-Y30R»	1,8 м
О5	потолок	окраска, Tikkurila Euro Power 7, глубокоматовая, подготовка Q3	Tikkurila F485 «Damask»	8,6 м²

Примечания


1. Размеры — в мм от чистовых поверхностей стен; условные обозначения и общие указания — лист 2.
2. Двери скрытого монтажа — полотно в плоскости стены, отделка стены по полотну, плинтус прерывается у короба (узел — на листе узлов).

					Проект: Квартира 56 м²
	Лист	№ док.	Подпись	Дата	Развёртка стены Г. Прихожая (пом. 5)
Дизайнер	Кырлан А.С.			19.10.26	


Стадия	Лист	Листов
П	48	56

выпуск 19.10.2026 № 60226ce68e · стр. 48 из 56


Вид с фасадами

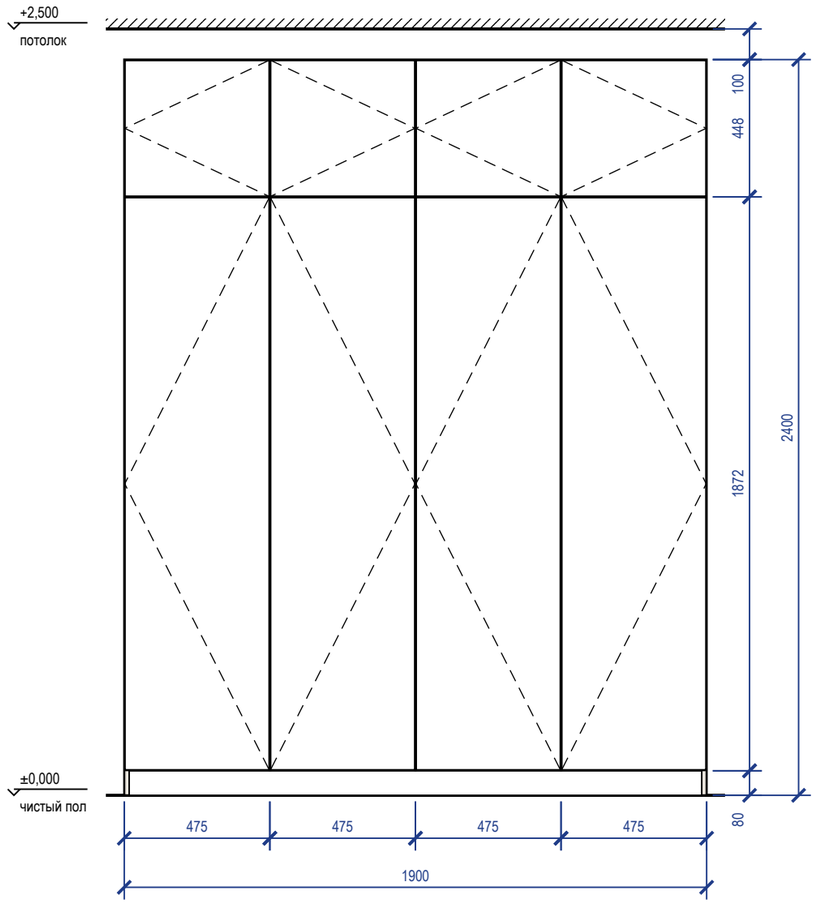


Вид без фасадов

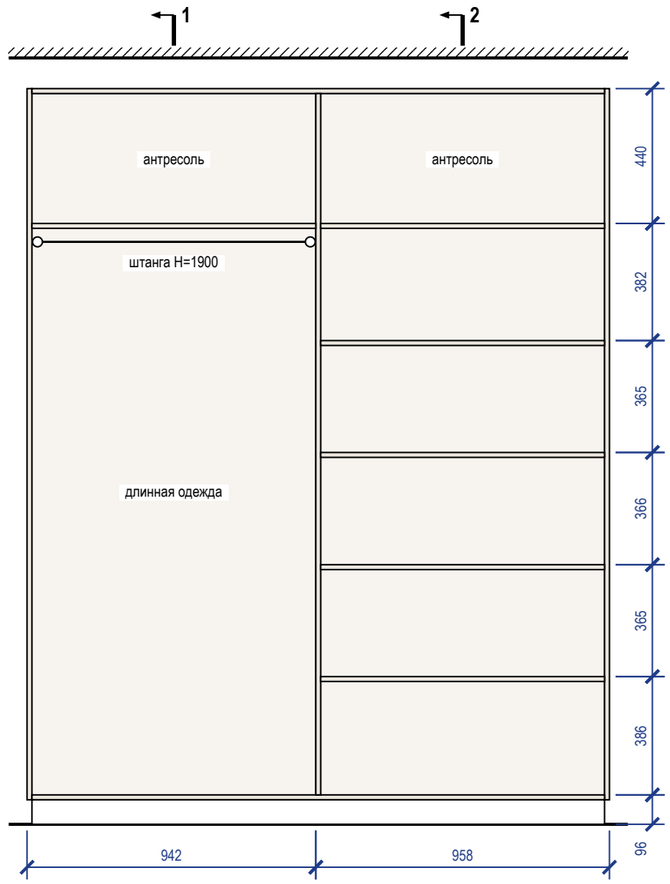

Разрез 1-1

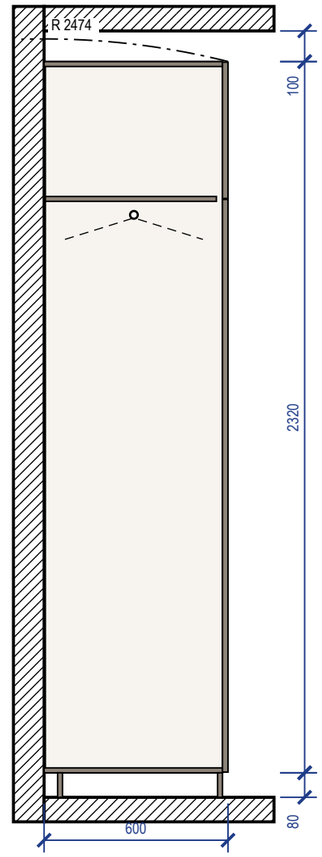


Разрез 2-2

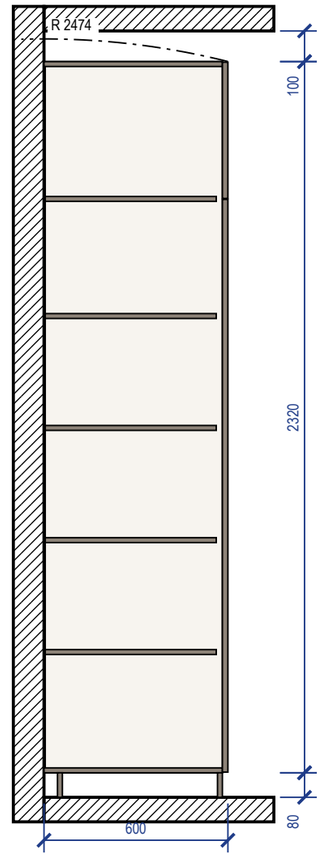

Примечания


1. Размеры — в мм по чистовой отделке; изделие 1900×600×2400 (Ш×Г×В). Перед раскроем — контрольный замер цеха после чистовой отделки стен, пола и потолка.
2. Корпус — ЛДСП 16 мм, задняя стенка ХДФ 4 мм в паз, цоколь 80 мм на регулируемых опорах; фасады — МДФ, эмаль матовая 18 мм накладные, цвет — по колерной карте; петли с доводчиком: фасад 1869 мм — 4 петли, фасад 445 мм — 2 петли.
3. Кромка: скрытые торцы 0,4 мм, видимые 2 мм (ПВХ/АБС).
4. Номинальные зазоры: между фасадами 3 мм, фасад — стена и фасад — потолок не менее 3 мм, фасад ящика — стойка 2 мм.
5. Ящики — направляющие полного выдвижения NL 550 (внутренняя глубина 578 мм ≥ NL + 3); присадка по 32-й системе — выполняет цех.
6. Зазор до потолка 100 мм — закрыть планкой в цвет корпуса при монтаже.
7. Подъём корпуса: диагональ боковины $\sqrt{(2400^2 + 600^2)} = 2474$ мм < 2500 мм до потолка — корпус собирается лёжа и поднимается поворотом.
8. Крепление к стене от опрокидывания: уголок к стене, 2 шт.; основание стены и шаг анкеров — монтажная схема шкафов.

3D орто

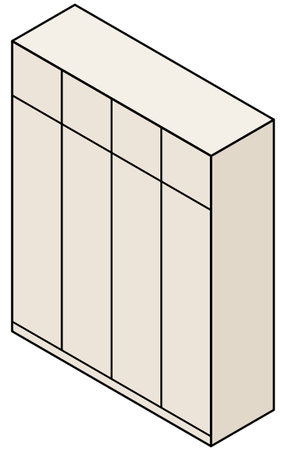


					Проект: Квартира 56 м²		
	Лист	№ док.	Подпись	Дата	Шкаф распашной М_19	Стадия	Лист	Листов
Дизайнер	Кырлан А.С.			19.10.26		П	Д_1	56


Вид с фасадами

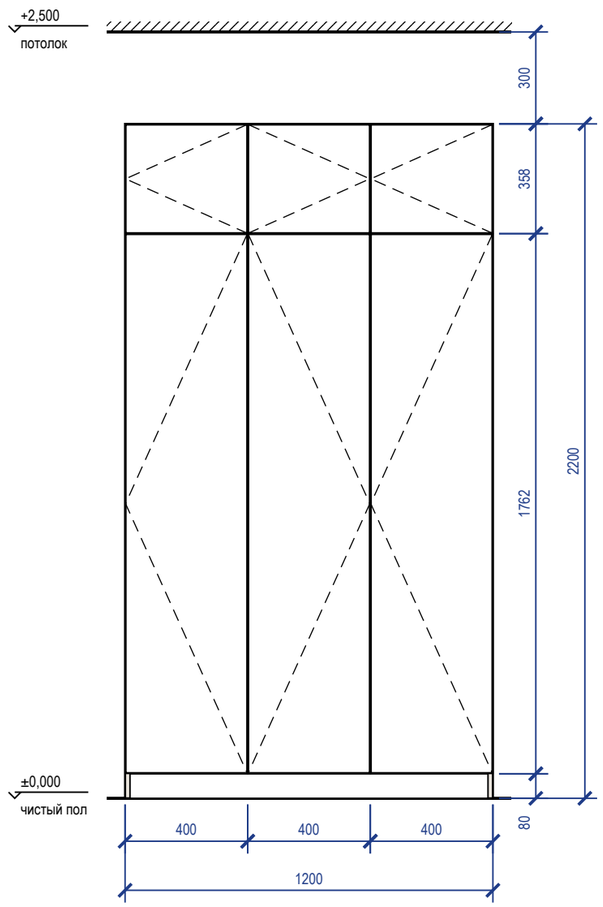


Вид без фасадов

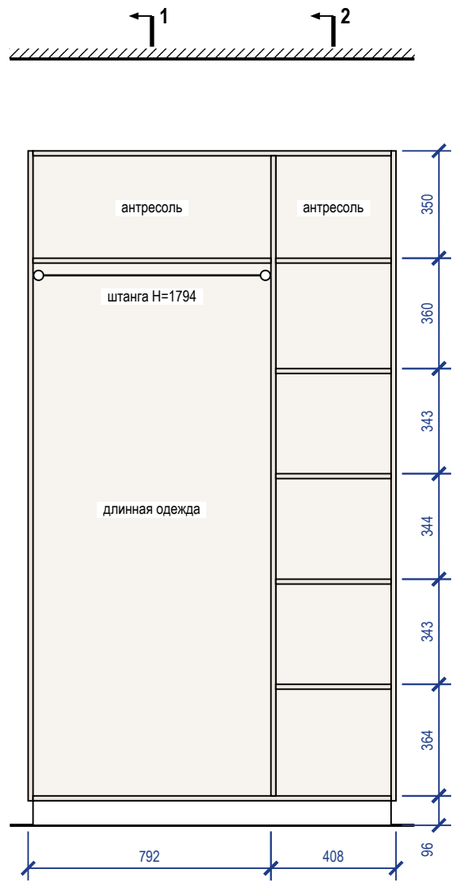

Разрез 1-1

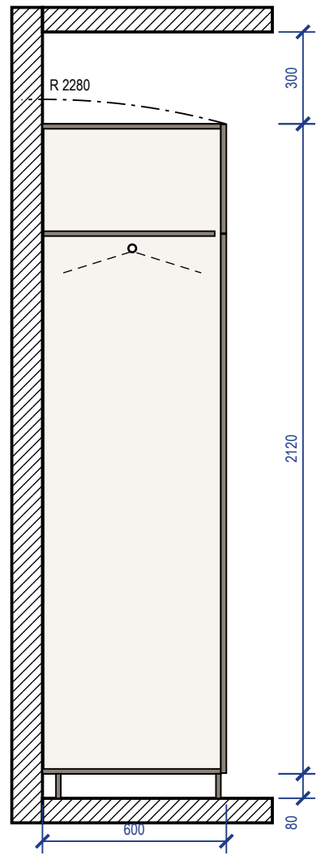


Разрез 2-2

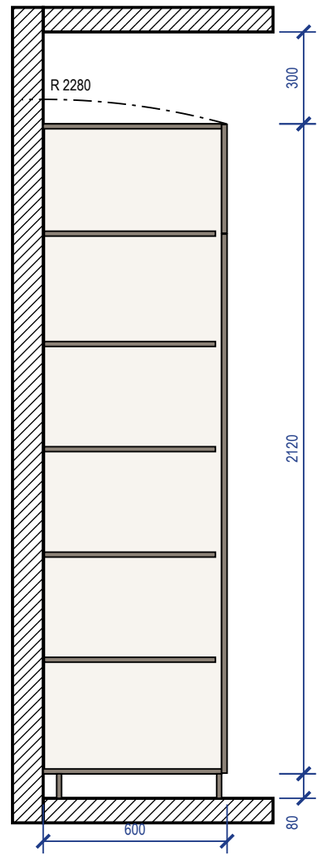

Примечания

1. Размеры — в мм по чистовой отделке; изделие 1200×600×2200 (Ш×Г×В). Перед раскроем — контрольный замер цеха после чистовой отделки стен, пола и потолка.
2. Корпус — ЛДСП 16 мм, задняя стенка ХДФ 4 мм в паз, цоколь 80 мм на регулируемых опорах; фасады — МДФ, эмаль матовая 18 мм накладные, цвет — по колерной карте; петли с доводчиком: фасад 1759 мм — 4 петли, фасад 355 мм — 2 петли.
3. Кромка: скрытые торцы 0,4 мм, видимые 2 мм (ПВХ/АБС).
4. Номинальные зазоры: между фасадами 3 мм, фасад — стена и фасад — потолок не менее 3 мм, фасад ящика — стойка 2 мм.
5. Ящики — направляющие полного выдвижения NL 550 (внутренняя глубина 578 мм ≥ NL + 3); присадка по 32-й системе — выполняет цех.
6. Зазор до потолка 300 мм.
7. Подъём корпуса: диагональ боковины $\sqrt{(2200^2 + 600^2)} = 2280$ мм < 2500 мм до потолка — корпус собирается лёжа и поднимается поворотом.
8. Крепление к стене от опрокидывания: уголок к стене, 2 шт.; основание стены и шаг анкеров — монтажная схема шкафов.

3D орто

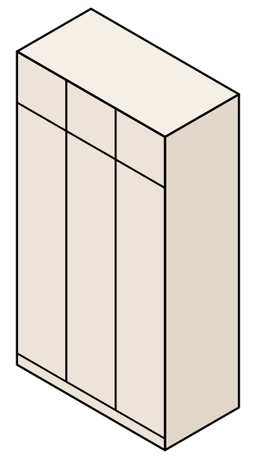


					Проект: Квартира 56 м²
	Лист	№ док.	Подпись	Дата	
Дизайнер	Кырлан А.С.			19.10.26	Шкаф распашной M_23


Стадия	Лист	Листов
П	Д_2	56

выпуск 19.10.2026 № 60226ce68e · стр. 50 из 56


Вид с фасадами

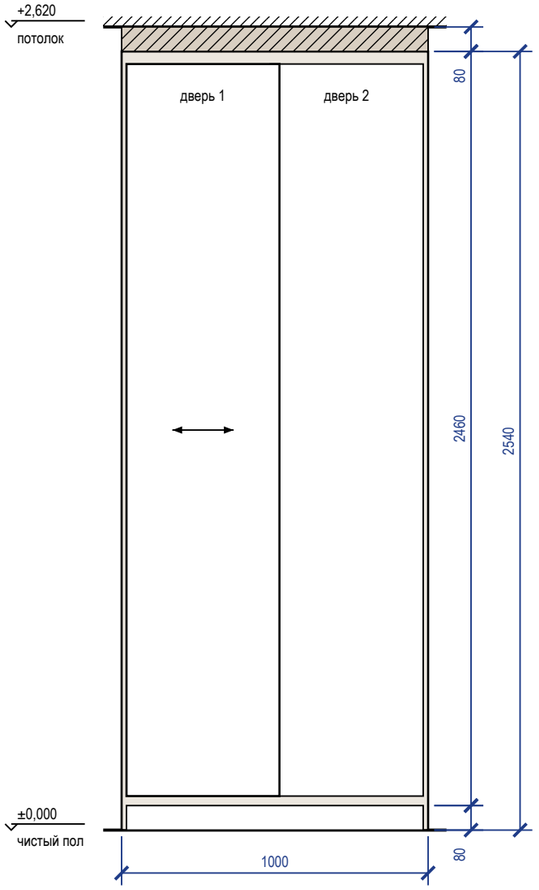


Вид без фасадов

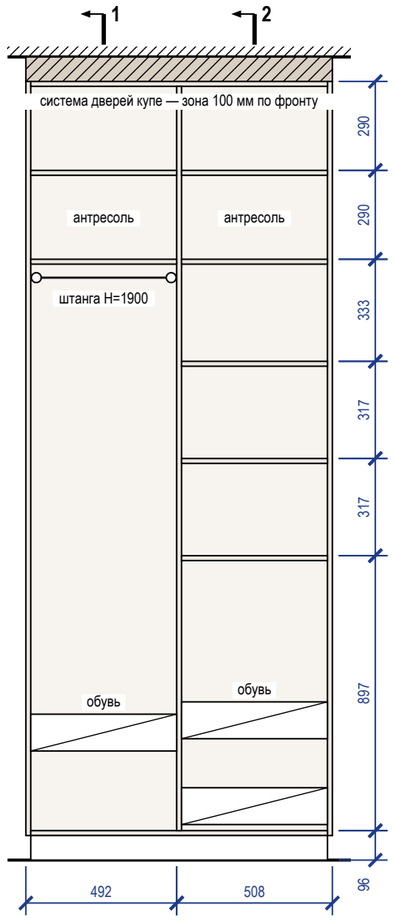

Разрез 1-1

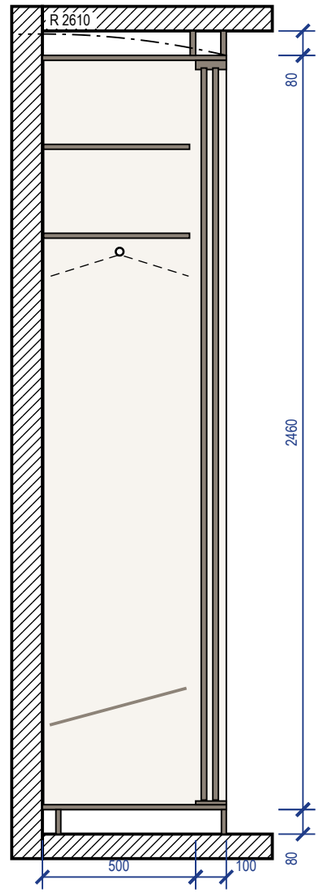


Разрез 2-2

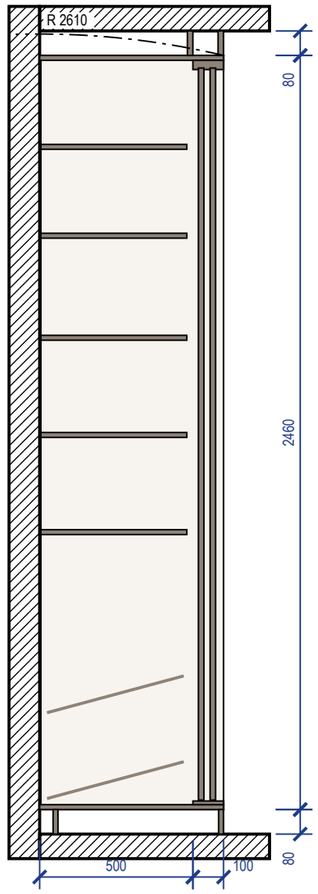

Примечания

1. Размеры — в мм по чистовой отделке; изделие 1000×600×2540 (Ш×Г×В). Перед раскроем — контрольный замер цеха после чистовой отделки стен, пола и потолка.
2. Корпус — ЛДСП 16 мм, задняя стенка ХДФ 4 мм в паз, цоколь 80 мм на регулируемых опорах; двери купе — ЛДСП 10 мм в алюминиевом профиле, нахлёст 30 мм, ширина двери 499 мм, высота — проём минус 40 мм; цвет — по колерной карте.
3. Кромка: скрытые торцы 0,4 мм, видимые 2 мм (ПВХ/АБС).
4. Номинальные зазоры: дверь купе — боковина 3 мм, фасад ящика — стойка 2 мм; ящики внутри купе — с накладкой 30 мм на стойке со стороны нахлёста дверей.
5. Ящики — направляющие полного выдвижения NL 450 (внутренняя глубина 496 мм ≥ NL + 3); присадка по 32-й системе — выполняет цех.
6. Компенсатор 80 мм — короб из ЛДСП по фронту и торцам, подгоняется к потолку при монтаже (припуск 20 мм), крепится к корпусу и к потолку.
7. Подъём корпуса: диагональ боковины $\sqrt{(2540^2 + 600^2)} = 2610$ мм < 2620 мм до потолка — корпус собирается лёжа и поднимается поворотом.
8. Крепление к стене от опрокидывания — уголки 2 шт. к несущему основанию (монтажная схема шкафов).


3D орто

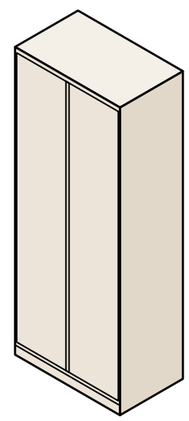


					Проект: Квартира 56 м²		
	Лист	№ док.	Подпись	Дата	Шкаф-купе M_27	Стадия	Лист	Листов
Дизайнер	Кырлан А.С.			19.10.26		П	Д_3	56

выпуск 19.10.2026 № 60226ce68e · стр. 51 из 56


Общий вид

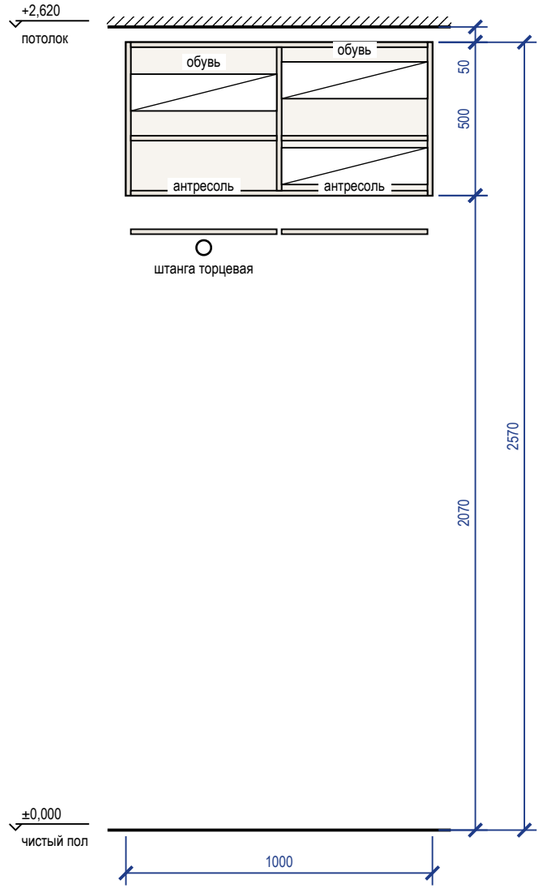


Наполнение, размеры в свету

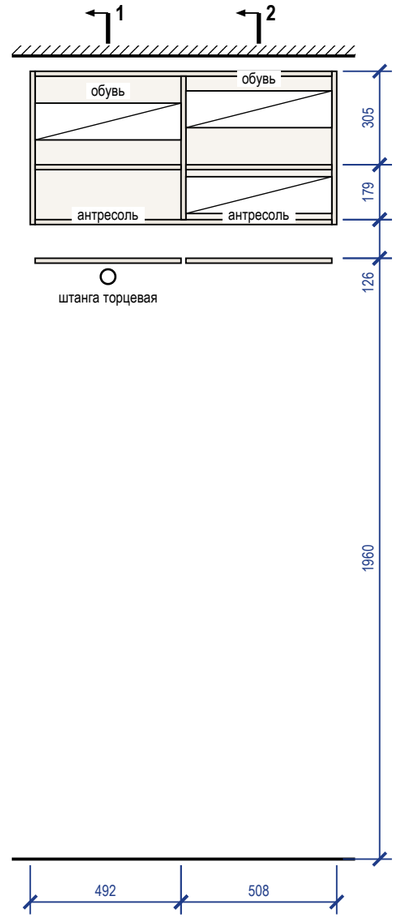

Разрез 1-1

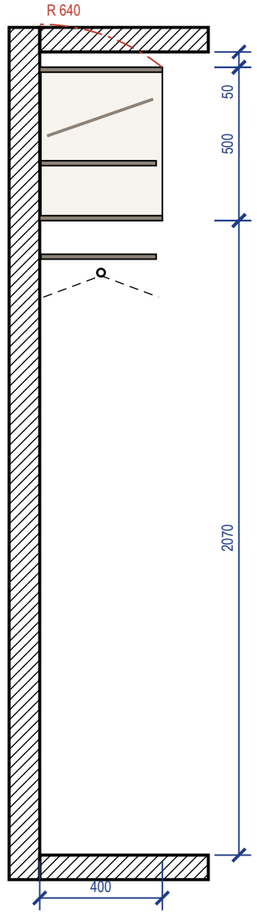


Разрез 2-2

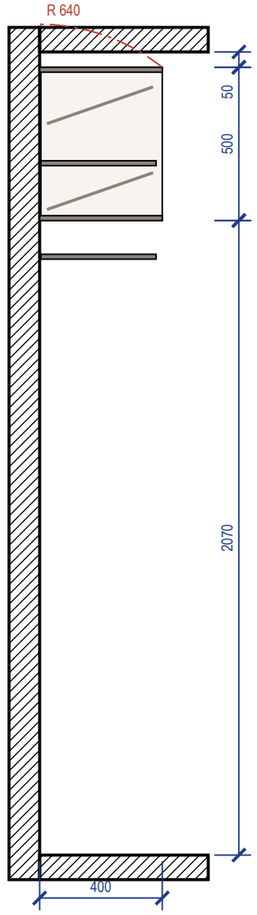

Примечания

1. Размеры — в мм по чистовой отделке; изделие 1000×400×500 (Ш×Г×В). Перед раскроем — контрольный замер цеха после чистовой отделки стен, пола и потолка.
2. Корпус — ЛДСП 16 мм, задняя стенка ХДФ 4 мм в паз, цоколь 0 мм на регулируемых опорах; открытая система без фасадов, ящики с фасадами.
3. Кромка: скрытые торцы 0,4 мм, видимые 2 мм (ПВХ/АБС).
4. Номинальные зазоры: между фасадами ящиков 3 мм, фасад ящика — стойка 2 мм.
5. Ящики — направляющие полного выдвижения NL 350 (внутренняя глубина 396 мм ≥ NL + 3); присадка по 32-й системе — выполняет цех.
6. Зазор до потолка 50 мм — закрыть планкой в цвет корпуса при монтаже.
7. Подъём корпуса (траектория на виде — красная: корпус не проходит под потолком): диагональ боковины $\sqrt{(500^2 + 400^2)} = 640$ мм > 550 мм до потолка — поднять собранный корпус нельзя: высота корпуса не более 360 мм, остальное — компенсатор, либо сборка стоя на месте.
8. Крепление к стене от опрокидывания: true; основание стены и шаг анкеров — монтажная схема шкафов.

3D орто

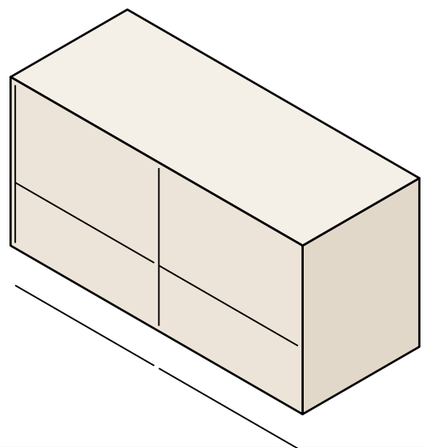


					Проект: Квартира 56 м²
	Лист	№ док.	Подпись	Дата	
Дизайнер	Кырлан А.С.			19.10.26	Система хранения M_29


Стадия	Лист	Листов
П	Д_4	56

выпуск 19.10.2026 № 60226ce68e · стр. 52 из 56


Вид с фасадами

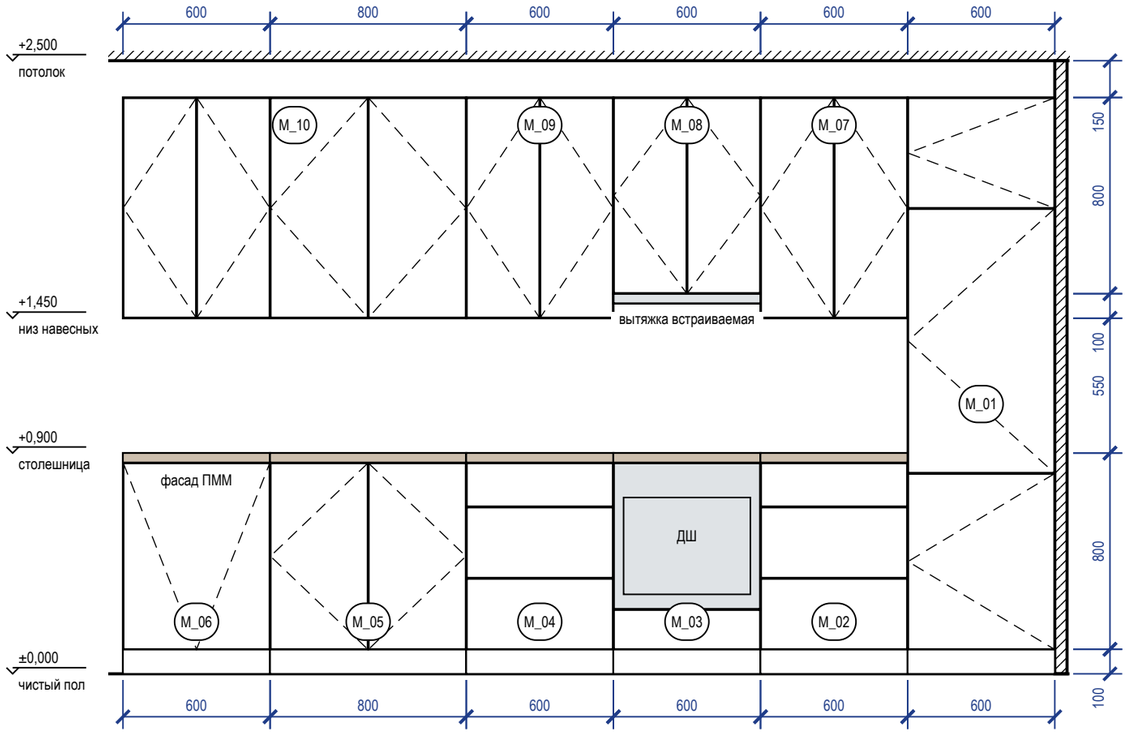


Вид без фасадов (наполнение, выводы)

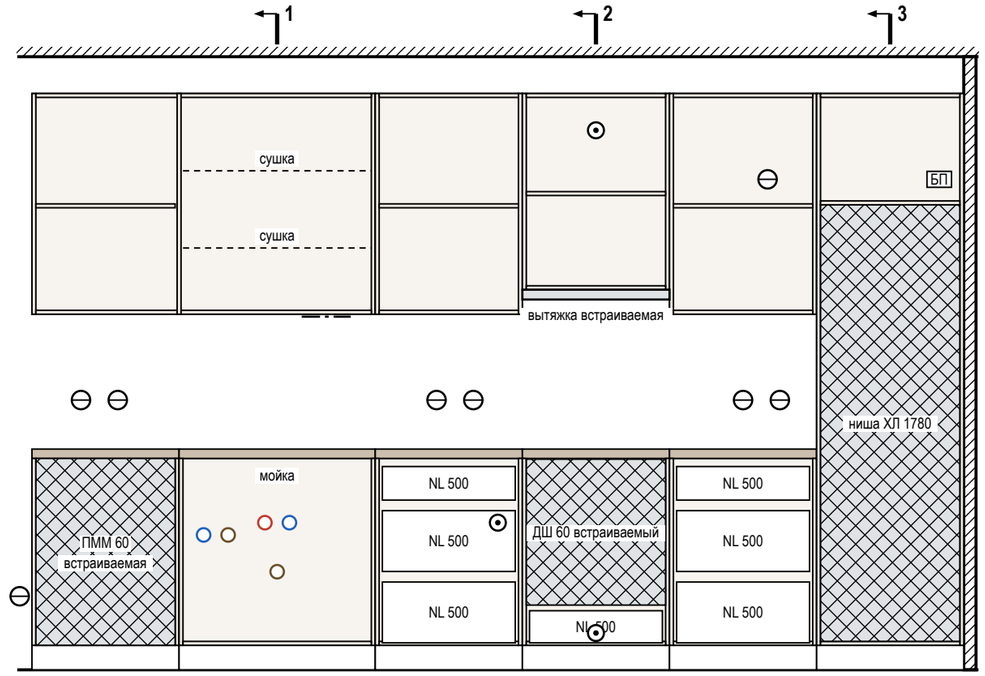


Разрез 1-1

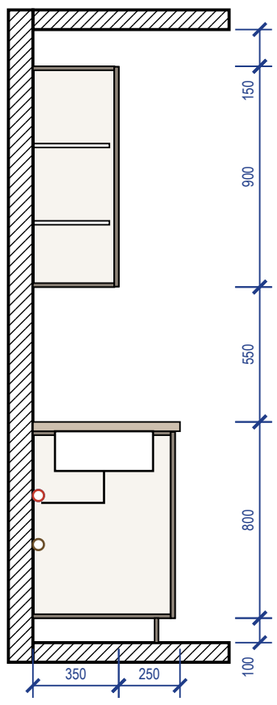


Разрез 2-2

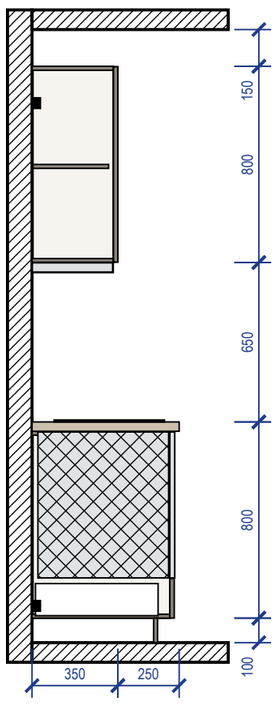

Разрез 3-3

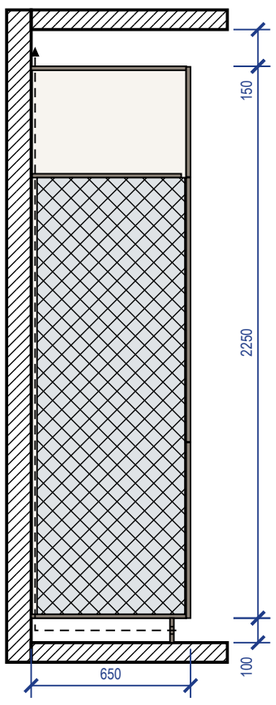

3D орто

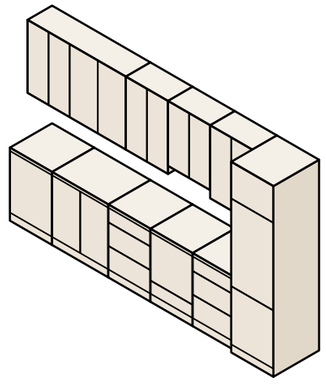

Примечания

1. Размеры — в мм по чистовой отделке, вид из помещения; марки — как на плане расстановки. Перед раскроем — контрольный замер цеха после фартука и пола.
2. Корпуса — ЛДСП 16 мм, задняя стенка ХДФ 4 мм; фасады — МДФ, эмаль матовая 18 мм, цвет по колерной карте; столешница 38 мм, свес 20 мм; цоколь 100 мм.
3. Кромка: скрытые торцы 0,4 мм, видимые 2 мм. Номинальные зазоры: между фасадами 3 мм, фасад — столешница 3 мм, фасад — стена не менее 3 мм.
4. Ящики полного выдвижения и петли — с доводчиком; присадка по 32-й системе — выполняет цех.
5. Вытяжка встраивается в навесной модуль над варочной: её низ 610 мм над панелью — меньше 650 мм, модуль поднять или принять вытяжку с допуском по паспорту модели.
6. Ниши техники (холодильник — ориентир 1780 мм) — по монтажным схемам выбранных моделей: решётка в цоколе и канал за пеналом холодильника, зазор за духовым шкафом, фасад ПММ на двери машины.

					Проект: Квартира 56 м²
	Лист	№ док.	Подпись	Дата	Кухня (пом. 1). Развёртка гарнитура
Дизайнер	Кырлан А.С.			19.10.26	

Стадия	Лист	Листов
П	Д_5	56

выпуск 19.10.2026 № 60226ce68e · стр. 53 из 56

Ведомость отделки помещений (форма 1 прил. А ГОСТ 21.501-2018)

№	Наименование помещения	Потолок			Стены и перегородки			Низ стен (плинтус)			Пол		Примечание
		Вид отделки	Код цвета	S, м²	Вид отделки	Код цвета	S, м²	Вид отделки	Код цвета	L, м	Вид отделки	S, м²	
1	Гостиная-кухня 20,80 м²	ГКЛ по каркасу П113, отм. +2,500; +2,600; окраска, Tikkurila Euro Power 7, глубокоматовая, 2 слоя, подготовка Q3	Tikkurila F485	20,80	Окраска, Tikkurila Euro Power 7, колеровка по NCS, матовая, 2 слоя, подготовка Q3 Акцент — стена А: окраска, Farrow & Ball Modern Emulsion, матовая, 2 слоя, подготовка Q3 Фартук кухни (стена Г): облицовка керамогранитом, аналог: керамогранит под травертин, матовый, 1200×600×9 мм, клей C2 TE S1, затирка CG2WA	NCS S 0804-Y30R Farrow & Ball No. 298 по артикулу	29,29 10,30 1,82	Плинтус МДФ h=80 мм, аналог: МДФ под покраску 80×16	NCS S 0804-Y30R	17,5	Инженерная доска, 1167-1101, 2100×127 мм, на клею; тип 1, отм. ЧП ±0,000	20,80	Н стен 2500 (до потолка); матовая моющаяся, класс 1 EN 13300 — осознанно вместо полуматовой; плинтус в цвет: стены
2	Спальня 13,60 м²	ГКЛ по каркасу П113, отм. +2,500; +2,600; окраска, Tikkurila Euro Power 7, глубокоматовая, 2 слоя, подготовка Q3	Tikkurila F485	13,60	Окраска, Tikkurila Euro Power 7, колеровка по NCS, матовая, 2 слоя, подготовка Q3 Акцент — стена А: окраска, Tikkurila Euro Power 7, колеровка по NCS, матовая, 2 слоя, подготовка Q3	NCS S 0804-Y30R NCS S 5010-G70Y	26,61 6,33	Плинтус МДФ h=80 мм, аналог: МДФ под покраску 80×16	NCS S 0804-Y30R	13,9	Инженерная доска, 1167-1101, 2100×127 мм, на клею; тип 1, отм. ЧП ±0,000	13,60	Н стен 2500 (до потолка); плинтус в цвет: стены
3	Детская 8,58 м²	ГКЛ по каркасу П113, отм. +2,500; +2,600; окраска, Tikkurila Euro Power 7, глубокоматовая, 2 слоя, подготовка Q3	Tikkurila F485	8,58	Окраска, Tikkurila Euro Power 7, колеровка по NCS, матовая, 2 слоя, подготовка Q3 Акцент — стена Г: окраска, Tikkurila Euro Power 7, матовая, 2 слоя, подготовка Q3	NCS S 0804-Y30R Tikkurila X447	19,29 6,50	Плинтус МДФ h=69 мм, SX165	NCS S 0804-Y30R	11,0	Инженерная доска, 1167-1101, 2100×127 мм, на клею; тип 1, отм. ЧП ±0,000	8,58	Н стен 2500 (до потолка); плинтус в цвет: стены
4	Санузел 4,81 м²	Окраска, Tikkurila Euro Power 7, матовая, 2 слоя, подготовка Q3	Tikkurila F485	4,81	Облицовка плиткой, A8UZ, 600×1200×9 мм, клей C2 TE S1, затирка CG2WA	Atlas Concorde A8UZ	19,93	нет			Керамогранит, A8UZ, 600×1200×9 мм; тип 2, отм. ЧП −0,015	4,81	Н стен 2715 (до потолка); гидроизоляция обмазочная, 2 слоя, с заведением на стены 200 мм (по пирогу пола); тест проливом и акт скрытых работ
5	Прихожая 8,58 м²	ГКЛ по каркасу П113, отм. +2,620; окраска, Tikkurila Euro Power 7, глубокоматовая, 2 слоя, подготовка Q3	Tikkurila F485	8,58	Окраска, Tikkurila Euro Power 7, колеровка по NCS, матовая, 2 слоя, подготовка Q3	NCS S 0804-Y30R	21,89	Плинтус МДФ h=80 мм, аналог: МДФ под покраску 80×16	NCS S 0804-Y30R	7,5	Керамогранит, A8UZ, 600×1200×9 мм; тип 3, отм. ЧП ±0,000	8,58	Н стен 2620 (до потолка); матовая моющаяся, класс 1 EN 13300 — осознанно вместо полуматовой; плинтус в цвет: стены
	Итого			**56,37**			**141,95**			**49,9**		**56,37**	

Сводка площадей по материалам отделки

Поверхность	Материал / код цвета	Серия	Площадь, м²
Потолок	Tikkurila F485	Euro Power 7	56,37
Стены	NCS S 0804-Y30R	Euro Power 7, колеровка по NCS	97,08
Стены	Farrow & Ball No. 298	Modern Emulsion	10,30
Стены	NCS S 5010-G70Y	Euro Power 7, колеровка по NCS	6,33
Стены	Tikkurila X447	Euro Power 7	6,50
Стены	облицовка плиткой 600×1200×9 мм, Atlas Concorde A8UZ	A8UZ	19,93
Фартук	облицовка керамогранитом 1200×600×9 мм	аналог: керамогранит под травертин, матовый	1,82

Примечания

1. Площади поверхностей — по чистым граням стен до отделки: стены = периметр × высоту от чистого пола помещения до низа потолка минус проёмы (облицовка плиткой — до верха облицовки); плинтус = периметр минус дверные проёмы; пол и потолок — по площади помещения. Количество плиток по раскладке. Площади помещений — с учётом всех частей помещения; откосы в площадь стен не входят.
2. Акцентные стены и фартук — отдельными строками, их площадь вычтена из основной отделки стен помещения; фартук — над нижними модулями кухни от столешницы до низа навесных шкафов, где шкафов нет — на 600 мм.
3. Плинтус — длина по периметру за вычетом дверных проёмов; примыкания к наличникам и встроенной мебели — по развёрткам.
4. Формат плитки — Ш×В×Т (ширина × высота в положении укладки × толщина), мм; на полу — вдоль стен А/В × вдоль стен Б/Г.
5. Коды цвета — по веерам производителей; колеровка каждой краски одной партией, проверка выкраса при свете D65 и при лампах проекта.
6. Уровни подготовки Q1–Q4 — система Knauf, не норма ГОСТ/СП; допуски поверхностей — по СП 71.13330.2017 (действующая редакция).
7. «аналог:» — изделие задано характеристиками, марку и артикул согласовать с заказчиком до закупки.

					Проект: Квартира 56 м²			
	Лист	№ док.	Подпись	Дата	Ведомость отделки помещений	Стадия	Лист	Листов
Дизайнер	Кырлан А.С.			19.10.26		П	С1	56

Поз.	Наименование и техническая характеристика	Тип, марка, обозначение документа	Код продукции	Поставщик	Ед. изм.	Кол.	Образец	Примечание
	Лакокрасочные материалы							
1	Краска интерьерная водно-дисперсионная акриловая для стен, матовая, класс мокрого истирания 1 по EN 13300, база A; цвет NCS S 0804-Y30R «S 0804-Y30R», колеровка машинная	Tikkurila Euro Power 7, колеровка по NCS		Tikkurila	л	27		поз. К1 колерной карты; пом. 1, 2, 3, 5; S = 97,1 м² × 2 сл. × 0,12 л/м² = 23,3 л, +10 % и 0,5 л на подкраску → ≥ 26,1 л; тара 3 × 9 л
2	Краска интерьерная водно-дисперсионная акриловая для акцентных стен, матовая, класс мокрого истирания 1 по EN 13300, база C; цвет Farrow & Ball No. 298 «Bancha», колеровка машинная	Farrow & Ball Modern Emulsion		Farrow & Ball	л	5		поз. К2 колерной карты; пом. 1; S = 10,3 м² × 2 сл. × 0,12 л/м² = 2,5 л, +10 % и 0,5 л на подкраску → ≥ 3,2 л; тара 1 × 5 л
3	Краска интерьерная водно-дисперсионная акриловая для потолков, глубокоматовая, класс мокрого истирания 2 по EN 13300, база A; цвет Tikkurila F485 «Damask», колеровка машинная	Tikkurila Euro Power 7		Tikkurila	л	14,4		поз. К3 колерной карты; пом. 1, 2, 3, 5; S = 51,6 м² × 2 сл. × 0,12 л/м² = 12,4 л, +10 % и 0,5 л на подкраску → ≥ 14,1 л; тара 1 × 9 л + 2 × 2,7 л
4	Краска интерьерная водно-дисперсионная акриловая для акцентных стен, матовая, класс мокрого истирания 1 по EN 13300, база C; цвет NCS S 5010-G70Y «S 5010-G70Y», колеровка машинная	Tikkurila Euro Power 7, колеровка по NCS		Tikkurila	л	2,7		поз. К5 колерной карты; пом. 2; S = 6,3 м² × 2 сл. × 0,12 л/м² = 1,5 л, +10 % и 0,5 л на подкраску → ≥ 2,2 л; тара 1 × 2,7 л
5	Краска интерьерная водно-дисперсионная акриловая для акцентных стен, матовая, класс мокрого истирания 1 по EN 13300, база C; цвет Tikkurila X447 «Sea Smoke», колеровка машинная	Tikkurila Euro Power 7		Tikkurila	л	2,7		поз. К6 колерной карты; пом. 3; S = 6,5 м² × 2 сл. × 0,12 л/м² = 1,6 л, +10 % и 0,5 л на подкраску → ≥ 2,2 л; тара 1 × 2,7 л
6	Краска интерьерная водно-дисперсионная акриловая для потолков, матовая, класс мокрого истирания 1 по EN 13300, база A; цвет Tikkurila F485 «Damask», колеровка машинная	Tikkurila Euro Power 7		Tikkurila	л	1,8		поз. К9 колерной карты; пом. 4; S = 4,8 м² × 2 сл. × 0,12 л/м² = 1,2 л, +10 % и 0,5 л на подкраску → ≥ 1,8 л; тара 2 × 0,9 л
7	Краска для МДФ и дерева в цвет NCS S 0804-Y30R «S 0804-Y30R» — окраска плинтуса; блеск не ниже блеска стен	марка не задана			л	1,3		поз. К4, К7; пом. 1, 2, 3, 5; L = 49,9 м, S = 4,7 м² × 2 сл. × 0,12 л/м² + 10 %; продукт подобрать в веере NCS
8	Грунтовка акриловая под окраску стен и потолков — из системы производителя краски	по системе краски			м²	177		площадь окраски стен, акцентов и потолков; 1 слой перед окраской; расход — по ТУ грунтовки
	Плитка и керамогранит							
9	Керамогранит под травертин, 600×600 мм	аналог по характеристикам			м²	6,12		шов 2 мм; Санузел, пол; по раскладке 15 шт (S = 4,81 м²), с запасом 17 шт
10	Керамогранит под травертин, 600×1200×9 мм, ректификат, водопоглощение 0,1 %	аналог по характеристикам		Atlas Concorde	м²	30,96		шов 2 мм; Санузел, стены А–Г; Санузел, короб инсталляции; по раскладке 38 шт (S = 20,73 м²), с запасом 43 шт
11	A8UZ, 600×1200×9 мм, ректификат, водопоглощение 0,1 % (BIa), противоскольжение R10, PEI IV	A8UZ		Atlas Concorde	м²	14,40		шов 2 мм; Прихожая, пол; по раскладке 18 шт (S = 8,58 м²), с запасом 20 шт
12	Керамогранит под травертин, матовый, 1200×600×9 мм, ректификат, водопоглощение 0,1 % (BIa)	аналог по характеристикам			м²	4,32		шов 2 мм; Гостиная-кухня, фартук (ст. Г); по раскладке 5 шт (S = 1,82 м²), с запасом 6 шт
	Напольные покрытия							
13	1167-1101, рабочий слой 4 мм, эмиссия E1, укладка на клей	1167-1101		Coswick	м²	46		пом. 1, 2, 3; S = 42,98 м² + 7 % (прямая укладка); к заказу — кратно упаковке
14	Клей для паркета и инженерной доски, эластичный (СМП / полиуретановый)	по рекомендации производителя доски			м²	43		площадь приклейки; расход и шпатель — по ТУ клея
	Погонажные изделия							
15	Плинтус МДФ под покраску 80×16, крепление к стене, окраска в цвет NCS S 0804-Y30R	аналог по характеристикам			м	43		пом. 1, 2, 5; L = 38,9 м (периметр без дверных проёмов) + 10 % на подрезку; в штуках — по длине планки
16	SX165, h = 69 мм, крепление к стене, окраска в цвет NCS S 0804-Y30R	SX165		Orac Decor	м	13		пом. 3; L = 11,0 м (периметр без дверных проёмов) + 10 % на подрезку; в штуках — по длине планки
	Смеси и материалы для облицовки							
17	Затирка для швов плитки, класс CG2WA по EN 13888	Mapei Ultracolor Plus 132		Mapei	кг	2,9		по раскладке (a+b)/(a·b) × шов × t × 1,6 + 10 %; в т. ч. 0,8 кг — позиции раскладки без марки
18	Клей плиточный C2 TE S1 по EN 12004, слой 5 мм	Ceresit CM 17		Ceresit	кг	288		12 меш. по 25 кг; 1,5 кг/м² на 1 мм слоя + 10 %; в т. ч. 85 кг — позиции раскладки без марки
19	Гидроизоляция обмазочная мокрых зон: пол, стены по периметру, зоны замачивания; 2 слоя с армирующей лентой в углах	аналог по характеристикам			м²	12,4		площадь по листу раскладки плитки + 10 %; расход смеси — по ТУ
20	Лента демпферная по периметру пола из плитки	аналог по характеристикам			м	16,9		периметр без дверных проёмов + 10 %

Примечания


1. Количества — из геометрии проекта: площади поверхностей по чистым граням стен до отделки (те же, что в ведомости отделки и колерной карте), плитка, клей и затирка — по раскладке плиточника; в графе «Кол.» — к заказу, с запасом.
2. Краска: расход 0,12 л/м² на слой в 2 слоя, если по ТУ не задан иной; запас 10 % и 0,5 л на подкраску каждого кода. Один код — одна партия, колеровка машинная в колеровочном центре бренда; в заказ — только после утверждения выкраса (колерная карта). Фасовка — по каталогу бренда на дату выпуска; к заказу — не меньше расчётного объёма.
3. «Аналог по характеристикам» — допускается изделие другого производителя с характеристиками не ниже указанных, по согласованию с автором проекта.
4. Графы «Код продукции» и «Масса 1 ед.» не заполнены: коды по классификатору продукции не присвоены, масса единицы до 25 кг (ГОСТ 21.110-2013).
5. Грунтовка и клей для доски указаны площадью обработки; объём — по ТУ выбранного продукта.

	Лист	№ док.	Подпись	Дата	
Дизайнер	Кырлан А.С.			19.10.26	Проект: Квартира 56 м²
					Спецификация отделочных материалов

Стадия	Лист	Листов
П	С2	56


1 Порог 15 мм: мокрая зона — жилое помещение (М 1:10)

Применение: двери Д-5

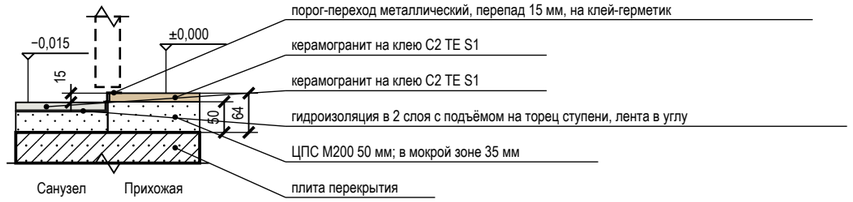


2 Стык покрытий пола Т-профилем без перепада (М 1:5)

Применение: проёмы 1↔5, 2↔5, 3↔5

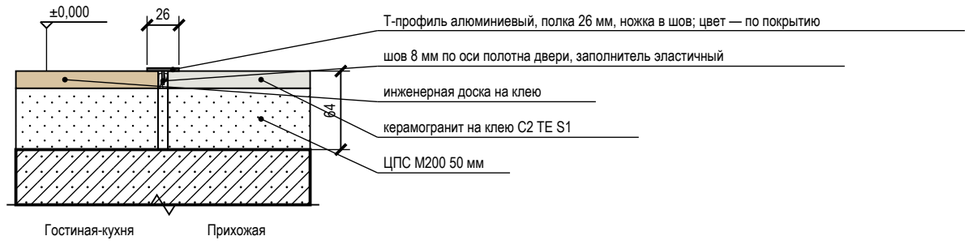


3 Дверь скрытого монтажа в плоскости стены, плинтус (М 1:5)

Применение: двери Д-2, Д-3, Д-4, Д-5

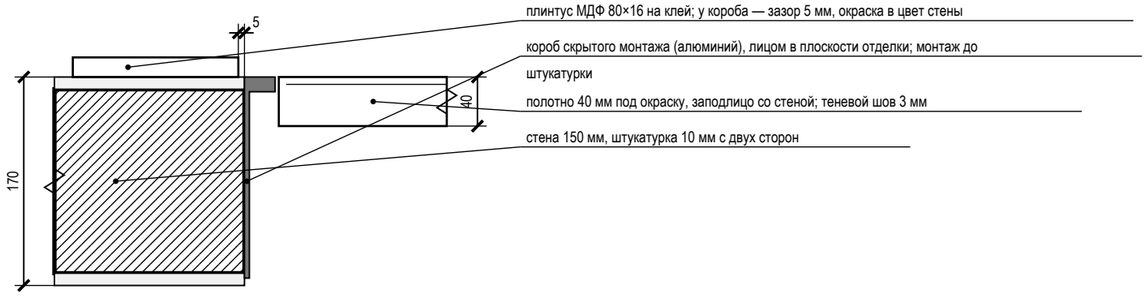


4 Короб стояков К1-1 с люком и звукоизоляцией (М 1:20)

Применение: пом. 4

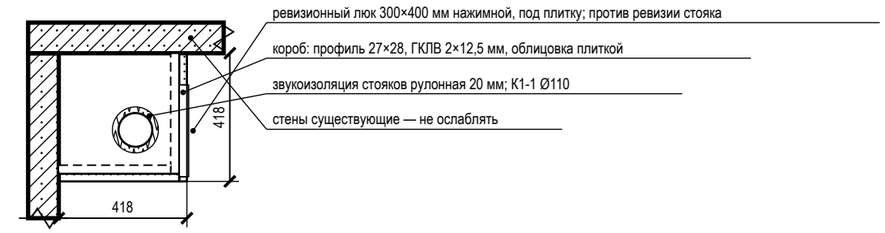


5 Гидроизоляция санузла: заход на стены 200 мм, примыкание ванны (М 1:20)

Применение: пом. 4

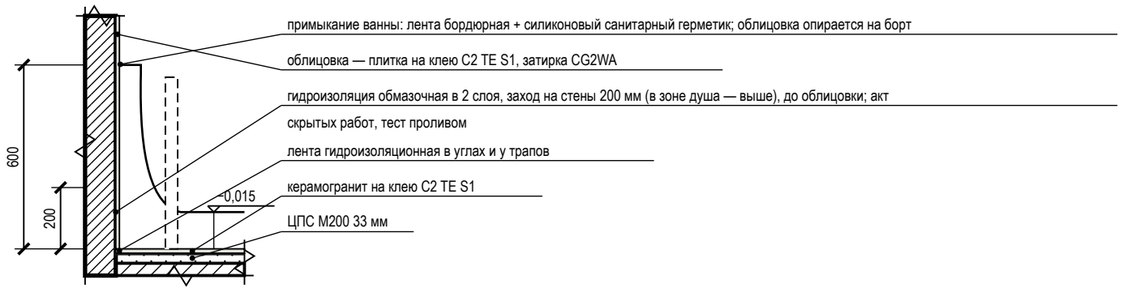

6 Плинтус МДФ 80×16 мм у окрашенной стены (М 1:10)

Применение: пом. 1, 2, 3, 5

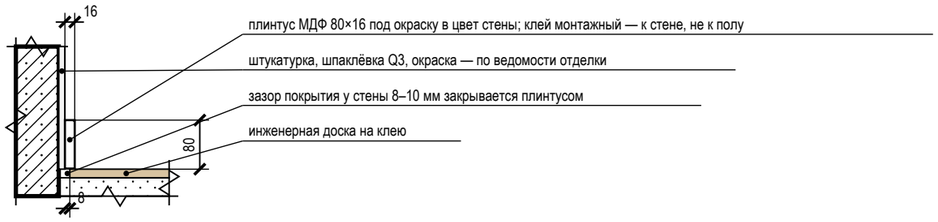

Условные обозначения

- железобетон (плита, стены)
- кладка, перегородка
- стяжка, раствор
- гипсокартон ГКЛВ
- звукоизоляция, эластичный заполнитель
- плитка, керамогранит на клею
- инженерная доска (покрытие пола)
- металлический профиль (порог, Т-профиль, короб двери)
- гидроизоляция (обмазочная, лента)

Примечания

1. Узлы — типовые решения проекта для мест, отмеченных выносками на листе схемы расположения развёрток и узлов; размеры — в мм, отметки — в м от ±0,000.
2. Узлы с гидроизоляцией, закладными и коробами скрытого монтажа принимаются по актам скрытых работ до закрытия отделкой; гидроизоляция — после теста проливом (24 ч).
3. Марки изделий (порог, Т-профиль, короб скрытой двери, люк) — по спецификациям; замена — на аналог с теми же габаритами по согласованию с автором проекта.

					Проект: Квартира 56 м²
	Лист	№ док.	Подпись	Дата	Узлы
Дизайнер	Кырлан А.С.			19.10.26	

Стадия	Лист	Листов
П	С3	56

выпуск 19.10.2026 № 60226ce68e · стр. 56 из 56