LINEA

РАБОЧАЯ ДОКУМЕНТАЦИЯ

Квартира 103 м²

ретро с авторской мебелью

Шифр комплекта ГД-2026-009-АИ

Стадия РП

Дата выпуска 18.10.2026

ПРЕДВАРИТЕЛЬНО · не для производства работ
открыто пунктов: 4 (реестр — л. 6)

ДИЗАЙНЕР

Кырлан Александр Сергеевич

Содержание

ПРЕДВАРИТЕЛЬНО · не для производства работ · открыто пунктов: 4 (реестр — л. 6)

03 Общие данные 11 л.

14 Архитектурные решения 3 л.

18 Планировочное решение 5 л.

24 Электрооборудование 8 л.

33 Отопление и вентиляция 2 л.

36 Водоснабжение и канализация 4 л.

41 Потолки и ГКЛ-конструкции 5 л.

47 Полы и отделка 9 л.

57 Декор и текстиль 15 л.

73 Развёртки и узлы 27 л.

101 Смета 7 л.

109 Визуализации 26 л.

ДИЗАЙН-ПРОЕКТ ИНТЕРЬЕРА

Квартира 103 м²

ретро с авторской мебелью

100,72 м²

оптимизм · функциональность · тёплое дерево · лёгкость · ретро без китча · связь с улицей · графичные акценты

Ретро 2026: mid-century 65 % + ар-деко (art-deco.json) 35 %. Стены — School House White No. 291 и кремовый S 1005-Y20R, потолки — белый S 0502-Y; второй план — орех и тик, оливковый Bancha No. 298, сине-серый Inchyra Blue No. 289; акценты — горчица S 2050-Y20R, терракота S 3050-Y70R, тил S 5030-B10G, изумрудный бархат S 5040-B90G; металл — латунь. Мебель — авторские модели середины века (как предложение, модели уточняются с заказчиком).

ПАЛИТРА 60 / 30 / 10

F&B No. 291	NCS S 1005-Y20R	NCS S 0502-Y	F&B No. 298	F&B No. 289
60 %	60 %	60 %	30 %	30 %

Визуализация 1 · Вид сверху (3D): планировка с мебелью, текстилем и декором

ОБЪЕКТ	ОБЩАЯ ПЛОЩАДЬ	ПОМЕЩЕНИЙ
Квартира 103 м²	100,72 м²	11, из них жилых 4
СТИЛЬ	**СТАДИЯ**	**ШИФР**
Мид-сенчури · ретро с авторской мебелью	Рабочий проект · предварительно	ГД-2026-009-АИ

АВТОР ПРОЕКТА

Кырлан Александр Сергеевич

Октябрь 2026

Изм.	Кол.уч	Лист	№ док.	Подп.	Дата
Разраб.		Кырлан А.С.			18.10.26
Пров.					
ГИП					
Н. контр.					
Утв.					

ГД-2026-009-АИ

Квартира 103 м²

Общая площадь 100,72* м² · * размеры со скана, не замерены (реестр — л. 6, К-1)

Дизайн-проект интерьера

Стадия	Лист	Листов
РП	1	96

Титульный лист

М б/м

Кырлан Александр Сергеевич

выпуск 18.10.2026 № 53dc234b8d · стр. 3 из 135

Общие данные

Комплект ГД-2026-009-АИ · Квартира 103 м² · ретро с авторской мебелью

ПРЕДВАРИТЕЛЬНО · не для производства работ · открыто пунктов: 4 (реестр — л. 6)

Ведомость рабочих чертежей основного комплекта ГД-2026-009-АИ

Лист	Наименование	Примечание
1	Титульный лист	
2	Общие данные	
3	Общие данные	
4	Общие данные	
5	Общие данные	
6	Открытые вопросы, принятые допущения и конфликты	
7	Задание на контрольный обмер и обследование. Лист 1 из 2	
8	Задание на контрольный обмер и обследование. Лист 2 из 2	
9	График закупок и работ. Лист 1 из 3	
10	График закупок и работ. Лист 2 из 3	
11	График закупок и работ. Лист 3 из 3	
12	Обмерный план	
13	План демонтажа и монтажа перегородок	
14	План дверей и ведомость заполнения проёмов	
15	Концепция интерьера	
16	План расстановки мебели	
17	Спецификация мебели и оборудования	
18	Спецификация мебели и оборудования (продолжение)	
19	Спецификация мебели и оборудования (продолжение)	
20	План розеток и электровыводов	
21	План освещения	
22	План выключателей и схема включения	
23	Ведомость электроточек и изделий	
24	Ведомость электроточек и изделий (продолжение)	
25	Однолинейная схема щита	
26	План принципиальных трасс	
27	План слаботочных сетей	
28	План вентиляции	
29	План отопления	
30	План выводов сантехники Допущения и предложения на листе. См. лист открытых вопросов (лист 6).	

Ведомость рабочих чертежей основного комплекта ГД-2026-009-АИ (продолжение)

Лист	Наименование	Примечание
31	Схема разводки водопровода и канализации	
32	Спецификация сантехнического оборудования	
33	Спецификация светильников и сценарии освещения	
34	План потолков	
35	Раскладка плитки. Планы полов	
36	Раскладка плитки. Прихожая-холл	
37	Раскладка плитки. Ванная. Развёртки стен	
38	Раскладка плитки. Ванная мастер. Развёртки стен	
39	План полов	
40	Ведомость отделки помещений. Лист 1 из 2	
41	Ведомость отделки помещений. Лист 2 из 2	
42	Колерная карта	
43	Колерная карта	
44	Спецификация отделочных материалов	
45	Спецификация отделочных материалов	
46	Концепция декора и визуализации	
47	План текстиля и декора	
48	Шторы и карнизы	
49	Ведомость текстиля	
50	Ведомость декора. Схемы развески	
51	Встроенная мебель. Схема расположения	
52	Система хранения К1	
53	Шкаф-купе П1	

Общие указания — лист 5: ±0,000 — чистый пол; несущие конструкции и сети дома — по отдельному проекту; скрытые работы — по актам. Открытые вопросы и допущения — лист 6.

Изм.	Кол.уч	Лист	№ док.	Подп.	Дата
Разраб.		Кырлан А.С.			18.10.26
Пров.					
ГИП					
Н. контр.					
Утв.					

ГД-2026-009-АИ

Квартира 103 м²

Общая площадь 100,72* м² · * размеры со скана, не замерены (реестр — л. 6, К-1)

Дизайн-проект интерьера

Стадия	Лист	Листов
РП	2	96

Общие данные

М б/м

Кырлан Александр Сергеевич

выпуск 18.10.2026 № 53dc234b8d · стр. 4 из 135

Общие данные

ПРЕДВАРИТЕЛЬНО · не для производства работ · открыто пунктов: 4 (реестр — л. 6)

Допущения и предложения на листе. См. лист открытых вопросов (лист 6).

Ведомость рабочих чертежей основного комплекта ГД-2026-009-АИ (продолжение)

Лист	Наименование	Примечание
54	Система хранения Пс1	
55	Шкаф распашной С2	
56	Шкаф распашной М4	
57	Кухня (пом. 5). Развёртка гарнитура	
58	Кухня (пом. 5). Монтажная схема	
59	Кухня (пом. 5). Развёртка гарнитура	
60	Кухня (пом. 5). Монтажная схема	
61	Шкафы. Монтажная схема	
62	Ведомости изделий, техники и фурнитуры	
63	Реестр марок отделки и позиций альбома	
64	Реестр марок отделки и позиций альбома (продолжение)	
65	Схема расположения развёрток и узлов	
66	Развёртки стен А, Б. Кабинет-библиотека (пом. 1)	
67	Развёртки стен В, Г. Кабинет-библиотека (пом. 1)	
68	Развёртки стен. Кладовая (пом. 2)	
69	Развёртки стен А, Б. Гостиная-столовая (пом. 3)	
70	Развёртки стен В, Г. Гостиная-столовая (пом. 3)	
71	Развёртки стен А, Б. Прихожая-холл (пом. 4)	
72	Развёртки стен В, Г. Прихожая-холл (пом. 4)	
73	Развёртка стены А. Кухня (пом. 5), кухонный фронт	
74	Развёртка стены Б. Кухня (пом. 5), кухонный фронт	
75	Развёртка стены В. Кухня (пом. 5), кухонный фронт	
76	Развёртка стены Г. Кухня (пом. 5)	
77	Развёртки стен А, Б. Ванная (пом. 6)	
78	Развёртка стены В. Ванная (пом. 6)	
79	Развёртка стены Г. Ванная (пом. 6)	
80	Развёртки стен. Постирочная (пом. 7)	
81	Развёртки стен А, Б. Спальня 2 (пом. 8)	
82	Развёртки стен В, Г. Спальня 2 (пом. 8)	
83	Развёртки стен А, Б, В. Коридор (пом. 9)	

Ведомость рабочих чертежей основного комплекта ГД-2026-009-АИ (продолжение)

Лист	Наименование	Примечание
84	Развёртка стены Г. Коридор (пом. 9)	
85	Развёртки стен А, Б. Спальня мастер (пом. 10)	
86	Развёртки стен В, Г1, Г2. Спальня мастер (пом. 10)	
87	Развёртки стен А, Б. Ванная мастер (пом. 11)	
88	Развёртки стен В, Г. Ванная мастер (пом. 11)	
89	Узлы	
90	Ведомость объёмов работ	
91	Ведомость объёмов работ (продолжение)	
92	Ведомость объёмов работ (окончание)	
93	Спецификация материалов	
94	Спецификация материалов (окончание)	
95	Смета ориентировочная	
96	Смета ориентировочная (окончание)	

Ведомость ссылочных и прилагаемых документов

Обозначение	Наименование	Примечание
	Ссылочные документы	
ГОСТ 21.201-2011	СПДС. Условные графические изображения элементов зданий, сооружений и конструкций	
ГОСТ 21.205-2016	СПДС. Условные обозначения элементов санитарно-технических систем	
ГОСТ 21.210-2014	СПДС. Изображения условные графические электрооборудования и проводок на планах	
ГОСТ 2.306-68	ЕСКД. Обозначения графические материалов и правила их нанесения на чертежах	

Общие указания — лист 5: ±0,000 — чистый пол; несущие конструкции и сети дома — по отдельному проекту; скрытые работы — по актам. Открытые вопросы и допущения — лист 6.

Изм.	Кол.уч	Лист	№ док.	Подп.	Дата
Разраб.		Кырлан А.С.			18.10.26
Пров.					
ГИП					
Н. контр.					
Утв.					

ГД-2026-009-АИ

Квартира 103 м²

Общая площадь 100,72* м² · * размеры со скана, не замерены (реестр — л. 6, К-1)

Дизайн-проект интерьера

Стадия	Лист	Листов
РП	3	96

Общие данные

М б/м

Кырлан Александр Сергеевич

выпуск 18.10.2026 № 53dc234b8d · стр. 5 из 135

Общие данные

Комплект ГД-2026-009-АИ · лист 3 общих данных (продолжение)

Ведомость ссылочных и прилагаемых документов (продолжение)

Обозначение	Наименование	Примечание
	Прилагаемые документы	
ГД-2026-009-АИ.В1	Визуализация. Вид сверху (3D): планировка с мебелью, текстилем и декором	альбом визуализаций
ГД-2026-009-АИ.В2	Визуализация. Визуализация «room-bath1-wB»	
ГД-2026-009-АИ.В3	Визуализация. Визуализация «room-bath1-wC»	
ГД-2026-009-АИ.В4	Визуализация. Визуализация «room-bath1-wD»	
ГД-2026-009-АИ.В5	Визуализация. Визуализация «room-bath2-wide»	
ГД-2026-009-АИ.В6	Визуализация. Визуализация «room-bedroom1-wA»	
ГД-2026-009-АИ.В7	Визуализация. Визуализация «room-bedroom1-wB»	
ГД-2026-009-АИ.В8	Визуализация. Визуализация «room-bedroom1-wD»	
ГД-2026-009-АИ.В9	Визуализация. Визуализация «room-bedroom2-wA»	
ГД-2026-009-АИ.В10	Визуализация. Визуализация «room-bedroom2-wB»	
ГД-2026-009-АИ.В11	Визуализация. Визуализация «room-bedroom2-wC»	
ГД-2026-009-АИ.В12	Визуализация. Визуализация «room-bedroom2-wD»	
ГД-2026-009-АИ.В13	Визуализация. Визуализация «room-corridor-wB»	
ГД-2026-009-АИ.В14	Визуализация. Визуализация «room-hall-wA»	
ГД-2026-009-АИ.В15	Визуализация. Визуализация «room-hall-wB»	
ГД-2026-009-АИ.В16	Визуализация. Визуализация «room-kitchen-wB»	
ГД-2026-009-АИ.В17	Визуализация. Визуализация «room-kitchen-wC»	
ГД-2026-009-АИ.В18	Визуализация. Визуализация «room-living-wA»	
ГД-2026-009-АИ.В19	Визуализация. Визуализация «room-living-wB»	
ГД-2026-009-АИ.В20	Визуализация. Визуализация «room-living-wC»	
ГД-2026-009-АИ.В21	Визуализация. Визуализация «room-living-wD»	
ГД-2026-009-АИ.В22	Визуализация. Визуализация «room-storage-wide»	
ГД-2026-009-АИ.В23	Визуализация. Визуализация «room-study-wA»	
ГД-2026-009-АИ.В24	Визуализация. Визуализация «room-study-wB»	
ГД-2026-009-АИ.В25	Визуализация. Визуализация «room-study-wD»	
ГД-2026-009-АИ.В26	Визуализация. Визуализация «room-wardrobe-wide»	

Состав дизайн-проекта

Раздел	Состав	Листы
Обложка	Дизайн-проект интерьера; Квартира 103 м²; автор проекта — Кырлан Александр Сергеевич	1 с.
Концепция	Стиль Мид-сенчури 65 % + Ар-деко 35 %: концепция интерьера, палитра и материалы (колерная карта — лист 42)	л. 15
Визуализации	26 изобр.: Вид сверху (3D): планировка с мебелью, текстилем и декором; Визуализация «room-bath1-wB»; Визуализация «room-bath1-wC»; Визуализация «room-bath1-wD»; Визуализация «room-bath2-wide»; Визуализация «room-bedroom1-wA»; Визуализация «room-bedroom1-wB»; Визуализация «room-bedroom1-wD»; Визуализация «room-bedroom2-wA»; Визуализация «room-bedroom2-wB»; Визуализация «room-bedroom2-wC»; Визуализация «room-bedroom2-wD»; Визуализация «room-corridor-wB»; Визуализация «room-hall-wA»; Визуализация «room-hall-wB»; Визуализация «room-kitchen-wB»; Визуализация «room-kitchen-wC»; Визуализация «room-living-wA»; Визуализация «room-living-wB»; Визуализация «room-living-wC»; Визуализация «room-living-wD»; Визуализация «room-storage-wide»; Визуализация «room-study-wA»; Визуализация «room-study-wB»; Визуализация «room-study-wD»; Визуализация «room-wardrobe-wide»	В1–В26
Рабочие чертежи	планы, развёртки, узлы (развёртки и узлы — листы 65–72, 77, 80–83, 85–89)	л. 1–96
Спецификации и ведомости	оборудование, изделия, отделка, электроточки	л. 14, 17–19, 23, 24, 32, 33, 40–45, 49, 50, 90–94

Допущения и предложения на листе

Основа листа: размеры сняты со скана обмерного плана KV design (см): часть подписей не читается, помещения выровнены по читаемым размерам; контрольный обмер не выполнен (К-1); высота потолка 2650 мм принята по отметкам обмера (Н = 2,50…2,66 м, ригель 2,28 м) — уточнить при обмере (К-2); толщины стен 300 / 120 мм приняты, межквартирная стена и колонны — по скану, не замерены (К-1); разрешённая мощность 15 кВт принята по типовым ТУ; при объединении двух квартир — переоформление ТУ (К-4).

См. лист открытых вопросов (лист 6, записи К-1, К-2, К-4).

Общие указания — лист 5: ±0,000 — чистый пол; несущие конструкции и сети дома — по отдельному проекту; скрытые работы — по актам. Открытые вопросы и допущения — лист 6.

Изм.	Кол.уч	Лист	№ док.	Подп.	Дата
Разраб.		Кырлан А.С.			18.10.26
Пров.					
ГИП					
Н. контр.					
Утв.					

ГД-2026-009-АИ

Квартира 103 м²

Общая площадь 100,72* м² · * размеры со скана, не замерены (реестр — л. 6, К-1)

Дизайн-проект интерьера

Стадия	Лист	Листов
РП	4	96

Общие данные

М б/м

Кырлан Александр Сергеевич

выпуск 18.10.2026 № 53dc234b8d · стр. 6 из 135

Общие данные

Комплект ГД-2026-009-АИ · лист 4 общих данных (продолжение)

Условные обозначения

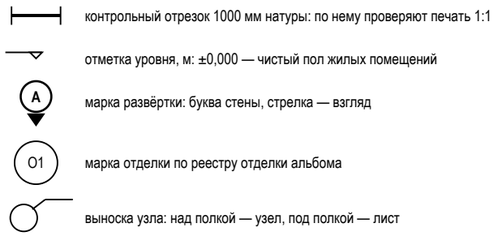

контрольный отрезок 1000 мм натуры: по нему проверяют печать 1:1

отметка уровня, м: ±0,000 — чистый пол жилых помещений

марка развёртки: буква стены, стрелка — взгляд

марка отделки по реестру отделки альбома

выноска узла: над полкой — узел, под полкой — лист

Общие указания

1. Рабочие чертежи интерьера разработаны на основании задания на проектирование и обмерного плана (лист 12). Объект: Квартира 103 м²; автор проекта — Кырлан Александр Сергеевич; общая площадь 100,72 м², жилая 64,79 м², помещений 11.
2. Рабочие чертежи выполнены в соответствии с заданием на проектирование и нормативными документами, перечисленными в п. 4.
3. Открытые вопросы, принятые допущения и конфликты между разделами, не снятые к выпуску комплекта, сведены в таблицы на листе 6. До ответа по пункту таблицы показанное на указанном там листе — допущение, а не утверждённое решение: комплект по этим листам предварительный.
4. Нормативные документы, на которые есть ссылки в листах комплекта: ГОСТ Р 21.101-2026; ГОСТ 21.501-2018; ГОСТ 2.302-68; ГОСТ 2.303-68; ГОСТ 2.304-81; ГОСТ 2.307-2011; СП 54.13330.2022; СП 71.13330.2017; СП 73.13330.2016; ПУЭ (7-е изд.), гл. 1.8, 7.1; ГОСТ Р 50571.7.701-2024; СанПиН 1.2.3685-21; ГОСТ 2.702; ГОСТ 2.755; ГОСТ 21.110-2013; ГОСТ 21.601; ГОСТ 13996-2019; ГОСТ 31565-2012; ГОСТ 31975; ГОСТ 32414-2013; ГОСТ 32415-2013; ГОСТ Р 56387-2018; ГОСТ Р 56926; СП 29.13330.2011; СП 30.13330.2020; СП 51.13330.2011; СП 52.13330.2016. Документы из ведомости ссылочных документов здесь не повторяются.
5. За отметку ±0,000 принят уровень чистого пола жилых помещений квартиры (относительная отметка; абсолютная — по проекту дома). Отметка чистого пола мокрых помещений — −0,015. Размеры — в миллиметрах, отметки — в метрах, площади — в м²; высоты установки Н от чистого пола своего помещения до оси изделия.
6. Несущие конструкции, общедомовые стояки, вентиляционные каналы и инженерные сети дома настоящим комплектом не изменяются. Работы, затрагивающие их (проём или штраба в несущей стене, перенос стояка, врезка в вентканал, расширение мокрой зоны), выполняются только по отдельному проекту, к которому прилагается техническое заключение о допустимости и безопасности работ, выданное автором проекта дома или организацией с допуском на обследование, и который согласован в установленном порядке (Жилищный кодекс РФ, ст. 25–29).
7. Трассы инженерных сетей на листах — принципиальные. Расчёты электрических нагрузок и токов КЗ, гидравлики, воздухообмена, освещённости и нагрузок на перекрытие выполняются в проектах ЭОМ, ВК, ОВ и КР организацией с допуском СРО; фактические трассы до закрытия отделкой фиксируются исполнительными схемами.
8. Стиль интерьера — Мид-сенчури 65 % + Ар-деко 35 %. Палитра проекта: основной 60 % — Farrow & Ball No. 291 «School House White — тёплый меловый белый», NCS S 1005-Y20R «Светлый кремовый», NCS S 0502-Y «Белый с лёгкой желтизной»; дополнительный 30 % Farrow & Ball No. 298 «Bancha — оливковый середины века», Farrow & Ball No. 289 «Inchyra Blue — тёмный сине-серый», Farrow & Ball No. 255 «Tanner's Brown — тёмный шоколад»; акцент 10 % — NCS S 2050-Y20R «Горчичный», NCS S 3050-Y70R «Терракотовый / жжёный оранжевый», NCS S 5030-B10G «Тил», NCS S 5040-B90G «Изумрудный». Коды цвета — по веерам производителей; цвет утверждается по выкрасу на объекте при освещении проекта.
9. Площади поверхностей — по чистым граням стен до отделки: стены = периметр × высоту от чистого пола помещения до низа потолка минус проёмы (облицовка плиткой — до верха облицовки); плинтус = периметр минус дверные проёмы; пол и потолок — по площади помещения. Количество плиток — по раскладке. Способ один для всех листов комплекта (ведомость отделки, колерная карта, раскладка плитки, развёртки).
10. Марки: стены помещения на всех листах — А (верхняя по плану), Б (правая), В (нижняя), Г (левая); марка отделки О — одна на весь альбом; реестр марок отделки (с позициями колерной карты той же отделки) и марки позиций по видам — на листе 63.
11. Развёртки стен выполнены по всем помещениям для стен с электроточками, мебелью, декором и отделкой: санузлы и кухонный фронт — в М 1:25, остальные стены — в М 1:40; расположение развёрток и узлов — на листе 65, узлы — на листе 89.
12. Перечень скрытых работ, на которые составляются акты освидетельствования (форма по приказу Минстроя России № 344/пр): гидроизоляция пола и стен мокрых помещений (с тестом проливом); стяжка пола (толщина, прочность, влажность основания); звукоизоляционные слои и демпферная лента; скрытая электропроводка (за потолком и в штробах стен; условия штробления — в следующем пункте); трубопроводы водоснабжения и канализации до закрытия (опрессовка, уклоны); закладные и усиления под подвесные приборы, мебель и тяжёлый декор, рамы инсталляций; короба дверей скрытого монтажа до штукатурки; каркасы ГКЛ потолков, коробов и перегородок до обшивки.
13. Скрытая электропроводка: за потолком и в штробах стен. Штробы в стенах выполняются только после технического заключения о несущих конструкциях; до заключения несущие стены не определены, и все стены считаются несущими; объём штроб — в ведомости объёмов работ, строка «Штробы в стенах» (вертикальные спуски; объём не меньше фактического, горизонтальные трассы — по исполнительной схеме).
14. Критерии приёмки: допуски отделочных покрытий — по СП 71.13330.2017; испытания систем водоснабжения и канализации — по СП 73.13330.2016 до закрытия трасс; приёмо-сдаточные испытания электроустановки — по ПУЭ, гл. 1.8, с протоколом электролаборатории.
15. Осознанные отступления от ГОСТ Р 21.101-2026, принятые в комплекте: номер листа и число листов («Листов») указаны на каждом листе; на масштабных листах в основной надписи указан фактический масштаб и дан контрольный отрезок 1000 мм; развёртки стен выполнены в М 1:25 и 1:40 (ГОСТ 21.507-81 — 1:50…1:500) ради читаемости привязок; размерные числа и марки элементов (Д-1, ОК-1, О6) — кеглем 2,5 мм, номера помещений — в кружке Ø 8 мм (канон — 3,5 мм и Ø 12 мм): так насыщенные листы А3 читаются без наложений надписей.
16. Графы «Пров.», «Н. контр.», «Утв.» основной надписи заполняются при согласовании комплекта с заказчиком; до согласования комплект подписывает автор проекта (графа «Разраб.»).

Допущения и предложения на листе

Основа листа: размеры сняты со скана обмерного плана KV design (см): часть подписей не читается, помещения выровнены по читаемым размерам; контрольный обмер не выполнен (К-1); высота потолка 2650 мм принята по отметкам обмера (Н = 2,50…2,66 м, ригель 2,28 м) — уточнить при обмере (К-2); толщины стен 300 / 120 мм приняты, межквартирная стена и колонны — по скану, не замерены (К-1); разрешённая мощность 15 кВт принята по типовым ТУ; при объединении двух квартир — переоформление ТУ (К-4).
См. лист открытых вопросов (лист 6, записи К-1, К-2, К-4).

						ГД-2026-009-АИ		
						Квартира 103 м²		
Изм.	Кол.уч	Лист	№ док.	Подп.	Дата	Общая площадь 100,72* м² · * размеры со скана, не замерены (реестр — л. 6, К-1)		
Разраб.		Кырлан А.С.			18.10.26	Дизайн-проект интерьера	Стадия: РП	Лист: 5 / Листов: 96
Пров.								
ГИП								
						Общие данные	**Кырлан Александр Сергеевич**	
Н. контр.						М б/м		
Утв.								

выпуск 18.10.2026 № 53dc234b8d · стр. 7 из 135

Открытые вопросы, принятые допущения и конфликты

Сводка по реестрам координации (стартовое совещание 18.10.2026)

Комплект предварительный по пунктам этих таблиц. Пока по пункту нет ответа или решения, показанное на указанном листе — допущение проектировщика, а не утверждённое решение.
Сводка: открытых вопросов — 4 (из них ждут факта объекта — 2: контрольного обмера, обследования или документа).
Пункты, ответ на которые лежит на объекте, а не за столом проектировщика (графа «Вид», строка «Ждёт»), собраны на листе «Задание на контрольный обмер и обследование» (листы 7, 8): что и где замерить, с какой точностью и чем подтвердить. Пункты, ждущие решения человека, на объекте не закрываются.

Открытые вопросы и принятые допущения

№	Формулировка	Вид	Кто решает	Если решения нет	Лист, где это проявляется
К-1	Размеры сняты со скана обмерного плана KV design (в см): часть подписей не читается, помещения выровнены по читаемым размерам. До заказа мебели, дверей и материалов нужен контрольный обмер.	Отсутствует Ждёт: обмера	Архитектор-планировщик	размеры на листах — по плану заказчика, уточняются по месту; мебель на заказ и материалы по ним не заказывать	л. 12 — Обмерный план л. 16 — План расстановки мебели
К-2	Высота потолка принята 2650 мм по отметкам обмера (Н = 2,50…2,66 м); под ригелем 2,28 м — уточнить.	Отсутствует	Архитектор-планировщик	высоты на развёртках и потолки — от 2650 мм, уточнить при обмере	л. 12 — Обмерный план л. 34 — План потолков
К-4	Разрешённая мощность объединённой квартиры по ТУ неизвестна, принята 15 кВт; при объединении двух квартир ТУ переоформляются.	Отсутствует	Инженер-электрик	щит и группы рассчитаны на 15 кВт; при меньших ТУ пересчёт	л. 25 — Однолинейная схема щита л. 20 — План розеток и электровыводов
К-5	Объединение двух квартир в одну (проём в межквартирной стене между гостиной и коридором правой квартиры, вход — один из тамбура, второй вход закрывается; правая кухня — постирочная) — предложение проектировщика. Межквартирная стена, колонны и ригель — несущие или нет, неизвестно (на обмере отмечены «несущие колонны» и «ригель перекрытия»): нужны поэтажный план БТИ, техзаключение и согласование перепланировки (ЖК РФ ст. 25–29).	Отсутствует Ждёт: документа	Архитектор-планировщик	проём и перегородки — предложение, к строительству не выдаются; мокрые зоны и кухня оставлены на местах обмера	л. 12 — Обмерный план

Примечания

1. Номера листов — по ведомости рабочих чертежей комплекта (лист «Общие данные»).
2. Графа «Если решения нет» показывает состояние решения на листах; влияние на сроки и стоимость по пунктам не оценивалось.
3. Пункт, по которому принято решение, при следующем выпуске комплекта из таблиц исключается.

Изм.	Кол.уч	Лист	№ док.	Подп.	Дата	ГД-2026-009-АИ		
						Квартира 103 м² Общая площадь 100,72* м² · * размеры со скана, не замерены (реестр — л. 6, К-1)		
Разраб.		Кырлан А.С.			18.10.26	Дизайн-проект интерьера	Стадия: РП	Лист: 6 / Листов: 96
Пров.								
ГИП								
Н. контр.						**Открытые вопросы, принятые допущения и конфликты** М б/м	**Кырлан Александр Сергеевич**	
Утв.								

ПРЕДВАРИТЕЛЬНО · не для производства работ · открыто пунктов: 4 (реестр — л. 6)

Задание на контрольный обмер и обследование. Лист 1 из 2

Что замерить, вскрыть и получить до заказа материалов и изделий

Задание собрано из открытых вопросов, ответ на которые лежит на объекте или в документах, а не за столом проектировщика. Пока факт не получен, размер, материал или положение на листах — допущение (знак «*»), а не замер.
Сводка: на объекте — 7 (до демонтажа — 5; после демонтажа — 2); документом и при закупке — 2; из допущений в данных и на листах — 8, из них без вопроса в реестре — 5. Закрываются вопросы: К-1, К-2, К-4, К-5 (4). Вопросы, ждущие решения человека, задание не закрывает — они решаются по реестру открытых вопросов.

Условия проведения

Порядок работ	Приёмы и точность	Кто присутствует	Если факт не совпал с проектом
1. До демонтажа — существующее состояние: контур, диагонали, высоты, проёмы, оси стояков, ниши и конструкции, которые видны. 2. После демонтажа, до черновых работ — то, что закрывали отделка и короба: основание стен, фактические толщины, углы, узлы. 3. Документы и данные закупки — не на объекте: к сроку из последней таблицы, от них зависят привязки и заказ. Что заказывается по размеру из задания, до закрытия пункта не заказывают: сроки изготовления — по графику закупок прораба.	Обход по часовой стрелке от входа: стены, проёмы, потолок, коммуникации (стояки, щиток, вентканалы), особенности (ниши, короба, выступы). Размеры записывают в мм; сумма участков равна общему размеру, при цепочке длиннее трёх участков ставят проверочный (общий) размер. Диагонали каждого помещения; если две диагонали различаются на 5 мм и больше, разницу подписывают на плане. Потолок — в нескольких точках: центр, углы, у проёмов. Проём — ширина, высота, глубина откоса, привязка к ближайшим углам, высота подоконника. Допустимая погрешность прибора — 2–3 мм на метр; размеры округляют кратно 5 мм; два контрольных промера одного размера не должны расходиться более чем на 2 %. Допуск по пункту — в графе «Точность». План БТИ обмер не заменяет.	Прораб (отвечает за проведение) — назначает день и порядок обхода, открывает объект и освобождает помещения, ведёт это задание и реестр изменений. Архитектор — выполняет обмер, составляет акт контрольного обмера и подписывает результаты по размерам и конструкциям. Владельцы вопросов присутствуют при пунктах своего раздела или принимают результат до заказа: Инженер ВК (вода, канализация) позиции О-1; Инженер-электрик — К-4; позиции О-2; Инженер ОВ позиции О-3; Отделочник — позиции О-6, О-7. Заказчик или его представитель — передаёт документы (план БТИ, проект дома, технические условия, паспорта), подписывает акт. Проектных решений на обмере не принимают: обмер даёт факт, решения — по реестру открытых вопросов (лист 6).	1. В пределах допуска пункта — принимается измеренное значение, лист перевыпускается, знак «*» снимается. 2. Больше допуска или контрольные промеры расходятся более чем на 2 % — промер повторяют; не подтвердилось — запись в реестр изменений (дата, лист, было, стало, кто решил, подпись), работы в этом месте не начинают. 3. Затронуты несущая стена, стояк, вентканал или мокрая зона — сразу владельцу раздела и ГИПу (главному инженеру проекта); между разделами не больше двух кругов, затем решает ГИП. 4. На объекте устно ничего не согласуется: каждое решение — записью в реестр с подписью.

Этап 1. До демонтажа

№	Где	Способ	Что сделать	Кто выполняет	Точность	Что пересчитается в альбоме	Чем подтверждается	Закрывает вопросы реестра
О-1	Ввод В1 и Т3 у стояков; по всей квартире	Обмер	Отключающая арматура и счётчики воды на вводах: положение, тип, пломбы управляющей компании. Альбом ставит их на каждом вводе по практике, в данных их нет.	Архитектор	±5 мм	Узлы ввода в спецификации ВК (краны, фильтры, счётчики); места ввода на плане выводов. Листы: л. 30 — План выводов сантехники л. 32 — Спецификация сантехнического оборудования	акт контрольного обмера; фото с рулеткой и привязкой к стене или углу	Вопроса в реестре нет: Альбом принимает счётчики воды на вводах без осмотра. Результат принимает: Инженер ВК (вода, канализация)
О-2	Вход в квартиру или лестничная клетка; место щита на плане	Обмер	Существующий щиток и счётчик электроэнергии: место и габарит ниши, состояние ввода, марка и сечение вводного кабеля, наличие вводного автомата и УЗО, пломбы.	Архитектор	±5 мм	Ниша и место щита на листах; вводной кабель и аппараты на однолинейной схеме; расстояния до первых групп. Листы: л. 25 — Однолинейная схема щита	акт контрольного обмера; фото с рулеткой и привязкой к стене или углу	Вопроса в реестре нет: Альбом принимает щит и ввод без осмотра. Результат принимает: Инженер-электрик
О-3	Кабинет-библиотека (пом. 1), Гостиная-столовая (пом. 3), Кухня (пом. 5), Спальня 2 (пом. 8), Спальня мастер (пом. 10); у окон	Обмер	Положение стояков отопления (подающий и обратный) от граней стен, диаметры, наличие запорной арматуры; существующие радиаторы: число секций, межосевое расстояние, подводки. В данных стояков отопления нет — лист отопления выводит их условно у откоса окна, радиаторы — «принципиально, по расчёту».	Архитектор	±5 мм	План отопления: места стояков и подводок, привязки радиаторов; подбор радиаторов по теплотехническому расчёту; радиаторы и узлы подключения в ВОР и спецификации. Листы: л. 29 — План отопления	акт контрольного обмера; фото с рулеткой и привязкой к стене или углу	Вопроса в реестре нет: Альбом принимает положение стояков и радиаторов отопления без обмера. Результат принимает: Инженер ОВ
О-4	все помещения	Обмер	Контрольный обмер всех помещений: стороны, диагонали, проёмы, высота потолка.	исполнитель	±5 мм; диагонали — разница от 5 мм подписывается	обмерный и монтажный планы, развёртки, мебель на заказ Листы: л. 12 — Обмерный план л. 16 — План расстановки мебели	акт контрольного обмера	К-1 Результат принимает: Архитектор

Допущения и предложения на листе
Основа листа: размеры сняты со скана обмерного плана KV design (см): часть подписей не читается, помещения выровнены по читаемым размерам; контрольный обмер не выполнен (К-1); высота потолка 2650 мм принята по отметкам обмера (Н = 2,50…2,66 м, ригель 2,28 м) — уточнить при обмере (К-2); толщины стен 300 / 120 мм приняты, межквартирная стена и колонны — по скану, не замерены (К-1); разрешённая мощность 15 кВт принята по типовым ТУ; при объединении двух квартир — переоформление ТУ (К-4).
См. лист открытых вопросов (лист 6, записи К-1, К-2, К-4).

Изм.	Кол.уч	Лист	№ док.	Подп.	Дата
Разраб.		Кырлан А.С.			18.10.26
Пров.					
ГИП					
Н. контр.					
Утв.					

ГД-2026-009-АИ

Квартира 103 м²

Общая площадь 100,72* м² · * размеры со скана, не замерены (реестр — л. 6, К-1)

Дизайн-проект интерьера

Стадия	Лист	Листов
РП	7	96

Задание на контрольный обмер и обследование.
Лист 1 из 2
М б/м

Кырлан Александр Сергеевич

выпуск 18.10.2026 № 53dc234b8d · стр. 9 из 135

Задание на контрольный обмер и обследование. Лист 2 из 2

ПРЕДВАРИТЕЛЬНО · не для производства работ · открыто пунктов: 4 (реестр — л. 6)

Что замерить, вскрыть и получить до заказа материалов и изделий

Этап 1. До демонтажа (продолжение)

№	Где	Способ	Что сделать	Кто выполняет	Точность	Что пересчитается в альбоме	Чем подтверждается	Закрывает вопросы реестра
О-5	Все помещения квартиры	Обмер	Высота потолка в каждом помещении в нескольких точках: центр, углы, у проёмов.	Архитектор	±5 мм	Вертикальные размеры альбома: развёртки, шкафы, плитка, объёмы работ. Листы: л. 2–5 — Общие данные	акт контрольного обмера	К-2 Результат принимает: Архитектор

Этап 2. После демонтажа, до черновых работ

№	Где	Способ	Что сделать	Кто выполняет	Точность	Что пересчитается в альбоме	Чем подтверждается	Закрывает вопросы реестра
О-6	Кабинет-библиотека (пом. 1), Кладовая (пом. 2), Гостиная-столовая (пом. 3), Прихожая-холл (пом. 4), Кухня (пом. 5), Ванная (пом. 6), Постирочная (пом. 7), Спальня 2 (пом. 8), Коридор (пом. 9), Спальня мастер (пом. 10), Ванная мастер (пом. 11)	Обмер	Нивелировка плиты перекрытия и существующего пола после демонтажа покрытий: отметки в углах и по сетке, перепады по помещению, уклоны, отметки порогов (чистый пол в мокрых зонах принят -15 мм, 0 мм). Принятая толщина стяжки 33 мм, 50 мм, 53 мм, 55 мм и отметка чистого пола — расчётные, не от замера плиты.	Архитектор	±5 мм по отметке; ровность просвет под 2-метровой рейкой, горизонталь против 0,2 % длины помещения	Толщина стяжки и отметка чистого пола; уклоны к трапам и пороги; выпуски К1 относительно чистого пола (план разводки); объёмы стяжки и смеси в ВОР и спецификации. Листы: л. 35, 39 — План полов л. 31 — Схема разводки водопровода и канализации	акт контрольного обмера	Вопроса в реестре нет: Альбом принимает отметки плиты и толщину пирога пола без нивелировки. Результат принимает: Отделочник
О-7	Кабинет-библиотека (пом. 1), Кладовая (пом. 2), Гостиная-столовая (пом. 3), Прихожая-холл (пом. 4), Кухня (пом. 5), Ванная (пом. 6), Постирочная (пом. 7), Спальня 2 (пом. 8), Коридор (пом. 9), Спальня мастер (пом. 10), Ванная мастер (пом. 11)	Обмер	Вертикаль и плоскостность стен: отклонение от вертикали по высоте стены (отвес или лазерный уровень), просвет под правилом 2 м, кривизна углов. Нужно там, где от стены зависит изделие: облицовка плиткой (пом. 6, 11), штукатурка и окраска (пом. 1, 2, 3, 4, 5, 6, 7, 8, 9, 10, 11), встроенная мебель и кухня (пом. 4, 5, 8, 10).	Архитектор	до 1 мм на 2 м (правило и клиновой щуп); вертикаль — мм на высоту стены, отклонения подписываются на плане	Толщина штукатурки и расход смеси в ВОР и спецификации; раскладка плитки (подрезка у стен); зазоры и крепление встроенной мебели и кухни. Листы: л. 35–38 — Раскладка плитки л. 40, 41 — Ведомость отделки помещений	акт контрольного обмера	Вопроса в реестре нет: Альбом принимает стены ровными и вертикальными без замера. Результат принимает: Отделочник

Документы и данные закупки (не на объекте)

№	У кого, откуда	Способ	Что получить	К какому сроку	Что пересчитается в альбоме	Чем подтверждается	Закрывает вопросы реестра
О-8	Заказчик; организация, выдавшая технические условия	Документ	Технические условия на присоединение: разрешённая мощность.	До утверждения однолинейной схемы щита	Однолинейная схема щита: вводной аппарат и группы. Листы: л. 2–5 — Общие данные	копия документа	К-4 Результат принимает: Инженер-электрик
О-9	вся квартира	Документ	Поэтажный план БТИ и техническое заключение о несущих стенах.	до демонтажа и возведения перегородок	монтажный план, проёмы, развёртки Листы: л. 12 — Обмерный план	копия документа	К-5 Результат принимает: Архитектор

Примечания

1. Подтверждение: акт контрольного обмера (дата, кто присутствовал, прибор, перечень промеров с результатами, подписи присутствующих); к акту — фото вскрытий и узлов и техническое заключение организации, выполнившей обследование.
2. Номера листов — по ведомости рабочих чертежей комплекта (лист «Общие данные»).
3. Пункт исключается из задания при следующем выпуске, когда акт подписан, значение внесено в проект и листы перевыпущены; знак «*» у величины снимается только замером.

Допущения и предложения на листе

Основа листа: размеры сняты со скана обмерного плана KV design (см): часть подписей не читается, помещения выровнены по читаемым размерам; контрольный обмер не выполнен (К-1); высота потолка 2650 мм принята по отметкам обмера (Н = 2,50…2,66 м, ригель 2,28 м) — уточнить при обмере (К-2); толщины стен 300 / 120 мм приняты, межквартирная стена и колонны — по скану, не замерены (К-1); разрешённая мощность 15 кВт принята по типовым ТУ; при объединении двух квартир — переоформление ТУ (К-4).
См. лист открытых вопросов (лист 6, записи К-1, К-2, К-4).

Изм.	Кол.уч	Лист	№ док.	Подп.	Дата
Разраб.		Кырлан А.С.			18.10.26
Пров.					
ГИП					
Н. контр.					
Утв.					

ГД-2026-009-АИ

Квартира 103 м²

Общая площадь 100,72* м² · * размеры со скана, не замерены (реестр — л. 6, К-1)

Дизайн-проект интерьера

Стадия	Лист	Листов
РП	8	96

Задание на контрольный обмер и обследование.
Лист 2 из 2
М б/м

Кырлан Александр Сергеевич

выпуск 18.10.2026 № 53dc234b8d · стр. 10 из 135

График закупок и работ. Лист 1 из 3

ПРЕДВАРИТЕЛЬНО · не для производства работ · открыто пунктов: 4 (реестр — л. 6)

Что заказывать и когда не раньше чего: относительный порядок без дат; срок поставки — из данных или «уточняется у поставщика»

Лист не содержит дат: контрольного обмера, подписанных решений автора и договоров ещё нет, и любая дата была бы выдумана. Вместо календаря — порядок и условия: замер → решение и выбор изделия → заказ → срок поставки → работа, которую позиция блокирует. Срок поставки печатается как срок, только если он задан в данных позиции. Нет — «срок уточняется у поставщика» и ссылка на вопрос реестра о сроках; типовой диапазон практики стоит рядом как ориентир и заказывать по нему нельзя. Номера З-N и Р-N — строки этого листа, К-N — записи реестра открытых вопросов, О-N — позиции задания на контрольный обмер.

Закупки: что заказывается, от чего зависит заказ и какую работу блокирует

№	Позиция и где	1. Замер до заказа	2. Решение, выбор изделия, паспорт	3. Условие заказа	4. Срок поставки	5. Блокирует работу	Закрывает вопросы реестра
З-1	Двери скрытого монтажа с коробом под покраску в существующих проёмах: Д-2, Д-3, Д-4, Д-5, Д-6, Д-7, Д-8, Д-9 — 8 шт. пом. 1, 2, 5, 6, 7, 8, 10, 11	О-4: обмер: все помещения (К-1); до заказа мебели и дверей		После 1 и 2 и после получения срока у поставщика (вопроса о сроках нет); дата заказа — когда срок известен, не позднее чем за срок до начала Р-5.	срок уточняется у поставщика Ориентир практики (не срок поставщика): ≈ 30 дн.	Р-5 «штукатурка»: короб ставят до штукатурки (коробку ставят на черновой стадии; полотно навешивают после чистовой отделки стен)	К-1
З-2	Кухонный гарнитур по проекту кухни: модули Кх1, Кх2, Кх3, Кх4, Кх7, Кх5 пом. 5			После 1 и 2 и после получения срока у поставщика (вопроса о сроках нет); дата заказа — когда срок известен, не позднее чем за срок до начала Р-15.	срок уточняется у поставщика Ориентир практики (не срок поставщика): 4–8 нед. от замера	Р-15 «кухня и мебель»: замер кухни — по готовым стенам после штукатурки или плитки, до чистового пола; производство идёт параллельно со стяжкой и отделкой	
З-3	Встраиваемая техника кухни: Кх2 посудомоечная машина, Кх5 холодильник пом. 5			После 1 и 2 и после получения срока у поставщика (вопроса о сроках нет); дата заказа — когда срок известен, не позднее чем за срок до начала Р-15.	срок уточняется у поставщика	Р-15 «кухня и мебель»: паспорта и монтажные схемы — до изготовления модулей кухни: нишу и вентзазоры задаёт модель, а не типовая схема 60 см	
З-4	Стиральная машина: Пс2 (вертикальная загрузка 400 × 600 мм — условие закупки) пом. 7			После 1 и 2 и после получения срока у поставщика (вопроса о сроках нет); дата заказа — когда срок известен, не позднее чем за срок до начала Р-4.	срок уточняется у поставщика	Р-4 «черновая сантехника»: габарит и подводка — до закрытия люка и разводки	
З-5	Сантехнические приборы и инсталляции: Сн1, Сн2, Сн3, См1, См2, См3 пом. 6, 11	О-3: обмер: Кабинет-библиотека (пом. 1), Гостиная-столовая (пом. 3), Кухня (пом. 5), Спальня 2 (пом. 8), Спальня мастер (пом. 10); у окон		После 1 и 2 и после получения срока у поставщика (вопроса о сроках нет); дата заказа — когда срок известен, не позднее чем за срок до начала Р-4.	срок уточняется у поставщика	Р-4 «черновая сантехника»: инсталляцию ставят до обшивки ГКЛВ и до гидроизоляции стены	
З-6	Керамогранит и плитка: 3 поз. по артикулу и формату, 51,07 м² по раскладке пом. 4, 6, 11	О-6: обмер: Кабинет-библиотека (пом. 1), Кладовая (пом. 2), Гостиная-столовая (пом. 3), Прихожая-холл (пом. 4), Кухня (пом. 5), Ванная (пом. 6), Постирочная (пом. 7), Спальня 2 (пом. 8), Коридор (пом. 9), Спальня мастер (пом. 10), Ванная мастер (пом. 11) О-7: обмер: Кабинет-библиотека (пом. 1), Кладовая (пом. 2), Гостиная-столовая (пом. 3), Прихожая-холл (пом. 4), Кухня (пом. 5), Ванная (пом. 6), Постирочная (пом. 7), Спальня 2 (пом. 8), Коридор (пом. 9), Спальня мастер (пом. 10), Ванная мастер (пом. 11)		После 1 и 2 и после получения срока у поставщика (вопроса о сроках нет); дата заказа — когда срок известен, не позднее чем за срок до начала Р-9.	срок уточняется у поставщика	Р-9 «плитка»: калибр партии измеряют до раскладки, раскладку пересчитывают до заказа	
З-7	Покрытие пола (доска) и плинтус: пом. 1, 2, 3, 5, 7, 8, 9, 10 пом. 1, 2, 3, 5, 7, 8, 9, 10	О-6: обмер: Кабинет-библиотека (пом. 1), Кладовая (пом. 2), Гостиная-столовая (пом. 3), Прихожая-холл (пом. 4), Кухня (пом. 5), Ванная (пом. 6), Постирочная (пом. 7), Спальня 2 (пом. 8), Коридор (пом. 9), Спальня мастер (пом. 10), Ванная мастер (пом. 11)		После 1 и 2 и после получения срока у поставщика (вопроса о сроках нет); дата заказа — когда срок известен, не позднее чем за срок до начала Р-12.	срок уточняется у поставщика	Р-12 «чистовые полы»: артикул и партия — до заказа; доску привозят к чистовым полам	

Допущения и предложения на листе

Основа листа: размеры сняты со скана обмерного плана KV design (см): часть подписей не читается, помещения выровнены по читаемым размерам; контрольный обмер не выполнен (К-1); высота потолка 2650 мм принята по отметкам обмера (Н = 2,50…2,66 м, ригель 2,28 м) — уточнить при обмере (К-2); толщины стен 300 / 120 мм приняты, межквартирная стена и колонны — по скану, не замерены (К-1); разрешённая мощность 15 кВт принята по типовым ТУ; при объединении двух квартир — переоформление ТУ (К-4).
См. лист открытых вопросов (лист 6, записи К-1, К-2, К-4).

Изм.	Кол.уч	Лист	№ док.	Подп.	Дата
Разраб.		Кырлан А.С.			18.10.26
Пров.					
ГИП					
Н. контр.					
Утв.					

ГД-2026-009-АИ

Квартира 103 м²

Общая площадь 100,72* м² · * размеры со скана, не замерены (реестр — л. 6, К-1)

Дизайн-проект интерьера

Стадия	Лист	Листов
РП	9	96

График закупок и работ. Лист 1 из 3

М б/м

Кырлан Александр Сергеевич

выпуск 18.10.2026 № 53dc234b8d · стр. 11 из 135

График закупок и работ. Лист 2 из 3

Что заказывать и когда не раньше чего: относительный порядок без дат; срок поставки — из данных или «уточняется у поставщика»

Закупки: что заказывается, от чего зависит заказ и какую работу блокирует (продолжение)

№	Позиция и где	1. Замер до заказа	2. Решение, выбор изделия, паспорт	3. Условие заказа	4. Срок поставки	5. Блокирует работу	Закрывает вопросы реестра
З-8	Встроенная мебель по замеру цеха: П1, С2, М4 пом. 4, 8, 10	О-4: обмер: все помещения (К-1); до заказа мебели и дверей		После 1 и 2 и после получения срока у поставщика (вопроса о сроках нет); дата заказа — когда срок известен, не позднее чем за срок до начала Р-15.	срок уточняется у поставщика Ориентир практики (не срок поставщика): 4–8 нед. от замера	Р-15 «кухня и мебель»: цех замеряет по готовым стенам; производство 4–8 недель идёт параллельно с отделкой	К-1

Работы: порядок и что не даёт начать

№	Работа (стадия технологической последовательности)	После	Что должно быть к началу: условия и закупки	Не начинать, пока открыто в реестре
Р-1	Демонтаж покрытий, отделки стен и потолков, дверных блоков и приборов; конструкции, стены и перегородки не трогать до технического заключения (стадия 1)		до начала: запрошены документы на дом и БТИ; контрольный обмер до демонтажа (что видно) сделан	
Р-2	Контрольный обмер на голых стенах и обследование (задание — лист «Задание на контрольный обмер») (стадия 2)	Р-1	после снятия отделки: видны стояки, каналы, щиток, толщины стен; до заказа всего, что делают по размеру	
Р-3	Черновая электрика: штробы, короба, гофра, подрозетники, щит (стадия 4)	Р-2	до начала: план электрики с высотами утверждён; штробы в стенах — только после технического заключения; мебель расставлена	К-4: Разрешённая мощность объединённой квартиры по ТУ неизвестна, принята 15 кВт; при объединении двух квартир ТУ переоформляются.
Р-4	Черновая сантехника и вентиляция: разводка, выводы, инсталляции, короба стояков (стадия 5)	Р-2	до начала: положение стояков замерено; модели инсталляций и машины выбраны (габариты рамы, подводка); инсталляцию ставят до обшивки ГКЛВ и до гидроизоляции Закупки к началу: З-4 (стиральная машина), З-5 (сантехника)	
Р-5	Коробки скрытых дверей, затем штукатурка стен и откосов (стадия 6)	Р-2, Р-3, Р-4	до начала: электрика и сантехника смонтированы, штробы заделаны; коробки скрытых дверей установлены до штукатурки (поэтому заказ дверей — раньше работы) Закупки к началу: З-1 (двери скрытого монтажа)	К-1: Размеры сняты со скана обмерного плана KV design (в см): часть подписей не читается, помещения выровнены по читаемым размерам.
Р-6	Стяжка пола и тёплый пол (стадия 7)	Р-5	до начала: штукатурка сделана; трубы под стяжкой приняты; нивелировка плиты выполнена	
Р-7	Гидроизоляция санузлов и тест проливом (стадия 8)	Р-6	до начала: стяжка набрала прочность и сухая по инструкции гидроизоляции; выводы стоят на проектных отметках	
Р-8	ГКЛ: короба инсталляции и стояков, ниши, потолки (стадия 9)	Р-3, Р-4	до начала: черновые сети в зоне коробов приняты; закладные под тяжёлое и карнизы стоят; светильники выбраны (вырезы)	
Р-9	Плитка и керамогранит: стены, затем пол; фартук (стадия 10)	Р-6, Р-7, Р-8	до начала: гидроизоляция принята; плитка выбрана, калибр партии измерен, раскладка пересчитана и подписана Закупки к началу: З-6 (плитка)	
Р-10	Шпаклёвка стен и потолков под окраску (стадия 11)	Р-5, Р-8, Р-9	до начала: плитка готова (грязные работы закончены); штукатурка и ГКЛ сухие	
Р-11	Окраска стен, потолков, откосов (стадия 13)	Р-10	до начала: шпаклёвка отшлифована и огрунтована; выкрасы утверждены, колеровка одной партией	
Р-12	Чистовые полы: инженерная доска (стадия 14)	Р-9, Р-11	до начала: влажность основания в норме, мокрые работы закончены; доска выбрана и привезена Закупки к началу: З-7 (доска и плинтус)	
Р-13	Полотна межкомнатных дверей, плинтусы, пороги (стадия 15)	Р-11, Р-12	до начала: чистовой пол уложен; полотна скрытых дверей — после чистовой отделки стен	

Допущения и предложения на листе

Основа листа: размеры сняты со скана обмерного плана KV design (см): часть подписей не читается, помещения выровнены по читаемым размерам; контрольный обмер не выполнен (К-1); высота потолка 2650 мм принята по отметкам обмера (Н = 2,50…2,66 м, ригель 2,28 м) — уточнить при обмере (К-2); толщины стен 300 / 120 мм приняты, межквартирная стена и колонны — по скану, не замерены (К-1); разрешённая мощность 15 кВт принята по типовым ТУ; при объединении двух квартир — переоформление ТУ (К-4).

См. лист открытых вопросов (лист 6, записи К-1, К-2, К-4).

Изм.	Кол.уч	Лист	№ док.	Подп.	Дата
Разраб.		Кырлан А.С.			18.10.26
Пров.					
ГИП					
Н. контр.					
Утв.					

ГД-2026-009-АИ

Квартира 103 м²

Общая площадь 100,72* м² · * размеры со скана, не замерены (реестр — л. 6, К-1)

Дизайн-проект интерьера

Стадия	Лист	Листов
РП	10	96

График закупок и работ. Лист 2 из 3

М б/м

Кырлан Александр Сергеевич

выпуск 18.10.2026 № 53dc234b8d · стр. 12 из 135

График закупок и работ. Лист 3 из 3

ПРЕДВАРИТЕЛЬНО · не для производства работ · открыто пунктов: 4 (реестр — л. 6)

Что заказывать и когда не раньше чего: относительный порядок без дат; срок поставки — из данных или «уточняется у поставщика»

Работы: порядок и что не даёт начать (продолжение)

№	Работа (стадия технологической последовательности)	После	Что должно быть к началу: условия и закупки	Не начинать, пока открыто в реестре
Р-14	Чистовая электрика и сантехника: механизмы, светильники, смесители, приборы (стадия 16)	Р-11, Р-13	до начала: отделка готова; механизмы, светильники и приборы выбраны и привезены	
Р-15	Кухня, встроенная и корпусная мебель, бытовая техника (стадия 17)	Р-13, Р-14	до начала: чистовая сантехника и электрика подведены к местам мебели; замер кухни снят по готовым стенам (после штукатурки или плитки, до чистового пола) Закупки к началу: З-2 (кухонный гарнитур), З-3 (техника кухни), З-8 (мебель по замеру)	К-1: Размеры сняты со скана обмерного плана KV design (в см): часть подписей не читается, помещения выровнены по читаемым размерам.
Р-16	Сдача: осмотр по чек-листу, дефектная ведомость, устранение замечаний (стадия 18)	Р-14, Р-15	до начала: всё смонтировано; акты скрытых работ подписаны	

Примечания

1. Порядок работ — стадии технологической последовательности из 16 позиций, присутствующих в этом проекте (по строкам ведомости объёмов); остальные стадии таблицы knowledge/remont-tehnologiya.md в проекте не встречаются. Длительности работ не печатаются: их нет ни в данных, ни в нормах для этого объекта.
2. Типовые сроки — ориентир практики, не срок поставщика: скрытые двери — короб около 10 дн., полотно под покраску до 3 нед., шпон 4–5 нед., в среднем около 30 дн. (knowledge/workers/foreman.md, п. 2.4 (profil-doors)); кухня и корпусная мебель — 4–8 недель от замера (knowledge/remont-tehnologiya.md, разд. 2; knowledge/workers/foreman.md, п. 2.4). Заказ по ориентиру не назначается: срок получают у поставщика (вопрос реестра), после чего заказ планируют «не позднее чем за срок до начала работы».
3. Условия заказа берутся из реестра открытых вопросов и задания на контрольный обмер: позиция заказывается, когда закрыты замер (графа 1) и решение (графа 2). Закрывать их может только факт или решение автора с подписью; снять строку с листа можно только закрыв запись реестра.
4. Заказ по размеру до контрольного обмера не делают: двери, кухня и встроенная мебель зависят от обмера (К-11, К-13); скрытые двери, кроме того, зависят от решения по нише санузла 2 (проём Д-5 в перегородке П-1).
5. Номера листов — по ведомости рабочих чертежей комплекта (лист «Общие данные»).

Допущения и предложения на листе

Основа листа: размеры сняты со скана обмерного плана KV design (см): часть подписей не читается, помещения выровнены по читаемым размерам; контрольный обмер не выполнен (К-1); высота потолка 2650 мм принята по отметкам обмера (Н = 2,50…2,66 м, ригель 2,28 м) — уточнить при обмере (К-2); толщины стен 300 / 120 мм приняты, межквартирная стена и колонны — по скану, не замерены (К-1); разрешённая мощность 15 кВт принята по типовым ТУ; при объединении двух квартир — переоформление ТУ (К-4).
См. лист открытых вопросов (лист 6, записи К-1, К-2, К-4).

Изм.	Кол.уч	Лист	№ док.	Подп.	Дата
Разраб.		Кырлан А.С.			18.10.26
Пров.					
ГИП					
Н. контр.					
Утв.					

ГД-2026-009-АИ

Квартира 103 м²

Общая площадь 100,72* м² · * размеры со скана, не замерены (реестр — л. 6, К-1)

Дизайн-проект интерьера

Стадия	Лист	Листов
РП	11	96

График закупок и работ. Лист 3 из 3

М б/м

Кырлан Александр Сергеевич

выпуск 18.10.2026 № 53dc234b8d · стр. 13 из 135

01

Архитектурные решения

Кырлан Александр Сергеевич

выпуск 18.10.2026 № 53dc234b8d · стр. 14 из 135

Обмерный план

Существующее положение · размеры в мм · отметки от чистого пола

ПРЕДВАРИТЕЛЬНО · не для производства работ · открыто пунктов: 4 (реестр — л. 6)

Отметки по высоте

±0,000	чистый пол пом. 1–5, 7–10; отсчёт высот
−0,015	чистый пол пом. 6, 11, ниже на 15 мм
плита*	верх плиты разный: −0,064, −0,170 (задание на обмер)
сущ. пол	снимается до плиты; не замерен (задание на обмер)

Принято, не определено или спорно

полностью — лист 6

К-5 — Объединение двух квартир в одну (проём в межквартирной стене между гостиной и коридором правой квартиры, вход — один из тамбура, второй вход закрывается; правая кухня — постирочная) предложение проектировщика

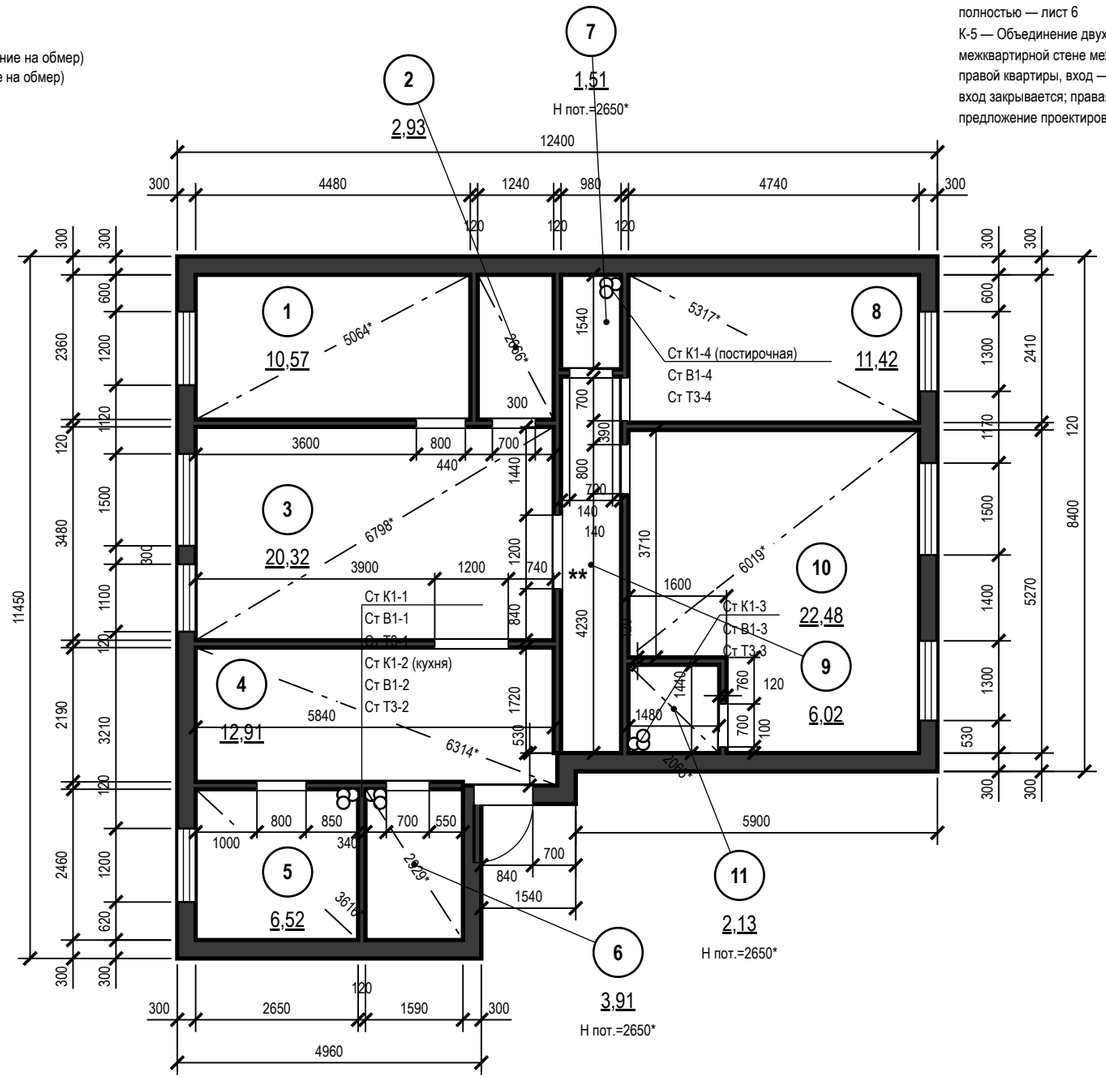

Экспликация помещений

№	Наименование	Площадь, м²
1	Кабинет-библиотека	10,57
2	Кладовая	2,93
3	Гостиная-столовая	20,32
4	Прихожая-холл	12,91
5	Кухня	6,52
6	Ванная	3,91
7	Постирочная	1,51
8	Спальня 2	11,42
9	Коридор	6,02
10	Спальня мастер	22,48
11	Ванная мастер	2,13
	Итого (общая площадь)	**100,72**

Условные обозначения

- существующие стены (сечение)
- окно (рама, остекление)
- проём существующий, без заполнения (откосы)
- стояк: К1 — канализация, В1 — ХВС, Т3 — ГВС
- ** — «**» — предложение проектировщика, заказчиком не утверждено
- диагональ помещения — контроль прямоугольности
- (1) — номер помещения, площадь м²

Примечания

1. Размеры — в мм по чистым поверхностям стен до отделки (по плану заказчика); площади — в м² по тем же размерам. До начала работ выполнить контрольный обмер.
2. Источник плана — допущение, не замер: растровый скан плана заказчика, размеры сняты с размерных цепочек, на объекте не замерены. Реестр: лист 6, вопрос К-1.
3. За отметку ±0,000 принят чистый пол, не существующий (блок отметок). Н пот. — высота от чистого пола до плиты перекрытия; Н пот. со знаком «*» — принятая высота, не замер (вопрос К-2).
4. Толщины стен: наружные 300 мм, перегородки 120 мм; отличающиеся толщины и уступы размерами на плане.
5. Несущие стены не определены: до технического заключения все стены считать несущими; проёмы и штробы в них не выполнять.
6. Дверные проёмы показаны без заполнения (двери — лист 14); высота дверных проёмов 2100 мм, проёмов без двери 2100 мм; низ окон (подоконник) 720, 735, 763, 783, 825 мм от чистого пола, высота окон 1560, 1550, 1552, 1548 мм.
7. Диагонали — контрольные размеры; «*» — расчёт по принятому контуру (К-1), при обмере заменить замеренным; расхождение более 5 мм подписать на плане как перекос.
8. Размеры проверить на месте до начала работ; расхождение контрольных промеров ≤ 2 %.
9. Размеры короче 1 мм на листе цепочкой не показаны (две выносные линии на таком расстоянии сливаются): пом. 9, стена Б — 20 мм от угла до проёма.

1000 мм · печать 1:1

Допущения и предложения на листе

Основа листа: размеры сняты со скана обмерного плана KV design (см): часть подписей не читается, помещения выровнены по читаемым размерам; контрольный обмер не выполнен (К-1); высота потолка 2650 мм принята по отметкам обмера (Н = 2,50…2,66 м, ригель 2,28 м) — уточнить при обмере (К-2); толщины стен 300 / 120 мм приняты, межквартирная стена и колонны — по скану, не замерены (К-1); разрешённая мощность 15 кВт принята по типовым ТУ; при объединении двух квартир — переоформление ТУ (К-4).

Знак «**» — предложение проектировщика, заказчиком не утверждено (согласовать с заказчиком): К-5: дверь пом. 3 (стена Б) — проём в межквартирной стене — объединение квартир, предложение до техзаключения.

Открытые вопросы и конфликты по листу: К-1, К-2, К-5.

См. лист открытых вопросов (лист 6, записи К-1, К-2, К-4, К-5).

Изм.	Кол.уч	Лист	№ док.	Подп.	Дата
Разраб.		Кырлан А.С.			18.10.26
Пров.					
ГИП					
Н. контр.					
Утв.					

ГД-2026-009-АИ

Квартира 103 м²

Общая площадь 100,72* м² · * размеры со скана, не замерены (реестр — л. 6, К-1)

Дизайн-проект интерьера

Стадия	Лист	Листов
РП	12	96

Обмерный план

М 1:100

Кырлан Александр Сергеевич

выпуск 18.10.2026 № 53dc234b8d · стр. 15 из 135

План демонтажа и монтажа перегородок

Перепланировка не выполняется · существующие стены сохраняются · размеры в мм

ПРЕДВАРИТЕЛЬНО · не для производства работ · открыто пунктов: 4 (реестр — л. 6)

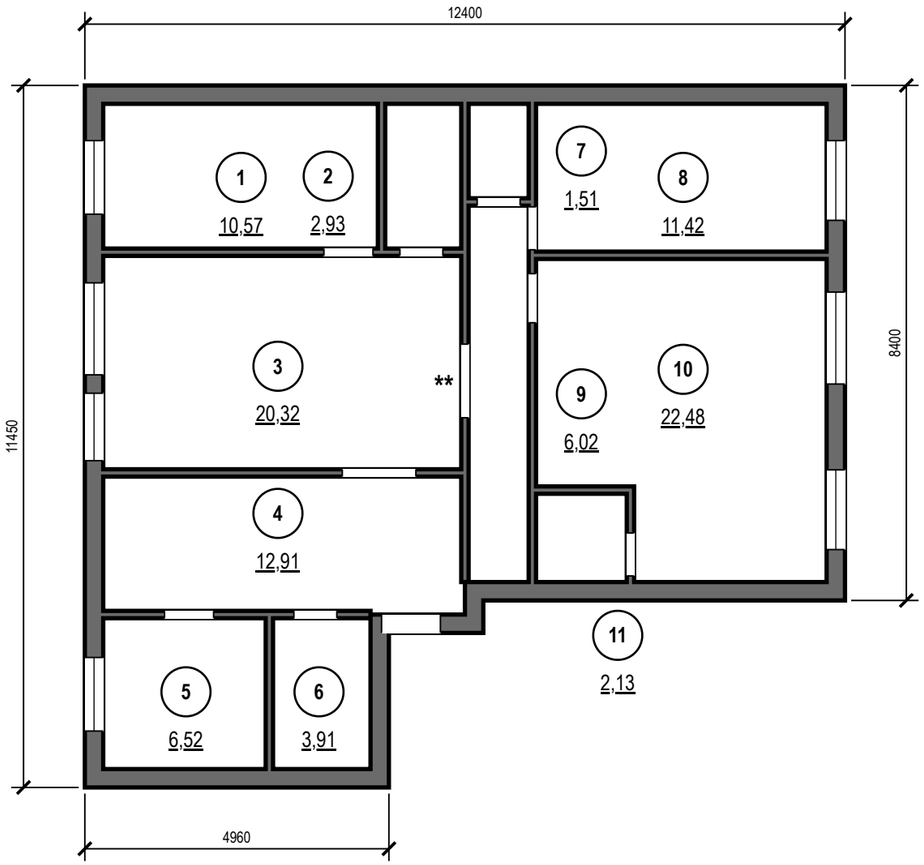

Условные обозначения

- существующие стены — сохраняются;
- несущие не определены — считать несущими
- демонтируемые конструкции — на плане нет
- возводимые перегородки — на плане нет
- проём существующий, без заполнения (откосы)
- (1) номер помещения, площадь м²

Отметки по высоте

±0,000	чистый пол пом. 1–5, 7–10; отсчёт высот	**плита***	верх плиты разный: −0,064, −0,170 (задание на обмер)
−0,015	чистый пол пом. 6, 11, ниже на 15 мм	**сущ. пол**	снимается до плиты; не замерен (задание на обмер)

Примечания

1. Перепланировка не выполняется: несущие и ненесущие стены, перегородки и плиты перекрытия не демонтируются, новые стены не возводятся; существующие стены и перегородки сохраняются.
2. Дверные блоки — по плану дверей (лист 14); существующие проёмы не расширяются.
3. Демонтаж существующих покрытий пола, стен и потолка, дверных блоков и сантехприборов (если есть) — до основания; объёмы демонтажа — для справки, по факту на объекте.
4. За отметку ±0,000 принят чистый пол, не существующий (блок отметок). Размеры — в мм по чистовой поверхности стен до отделки.
5. Размеры проверить на месте до начала работ: расхождение с обмером — не более 2 % (иначе — к архитектору).
6. Несущие стены не определены: до технического заключения все стены считать несущими — проёмы, ниши и штробы в них не выполнять.

Допущения и предложения на листе

Основа листа: размеры сняты со скана обмерного плана KV design (см): часть подписей не читается, помещения выровнены по читаемым размерам; контрольный обмер не выполнен (К-1); высота потолка 2650 мм принята по отметкам обмера (Н = 2,50…2,66 м, ригель 2,28 м) — уточнить при обмере (К-2); толщины стен 300 / 120 мм приняты, межквартирная стена и колонны — по скану, не замерены (К-1); разрешённая мощность 15 кВт принята по типовым ТУ; при объединении двух квартир — переоформление ТУ (К-4).

Знак «**» — предложение проектировщика, заказчиком не утверждено (согласовать с заказчиком): К-5: дверь пом. 3 (стена Б) — проём в межквартирной стене — объединение квартир, предложение до техзаключения.

См. лист открытых вопросов (лист 6, записи К-1, К-2, К-4, К-5).

1000 мм · печать 1:1

Изм.	Кол.уч	Лист	№ док.	Подп.	Дата
Разраб.		Кырлан А.С.			18.10.26
Пров.					
ГИП					
Н. контр.					
Утв.					

ГД-2026-009-АИ

Квартира 103 м²

Общая площадь 100,72* м² · * размеры со скана, не замерены (реестр — л. 6, К-1)

Дизайн-проект интерьера

Стадия	Лист	Листов
РП	13	96

План демонтажа и монтажа перегородок

М 1:100

Кырлан Александр Сергеевич

выпуск 18.10.2026 № 53dc234b8d · стр. 16 из 135

План дверей и ведомость заполнения проёмов

Проёмы, марки заполнения, привязки · размеры в мм

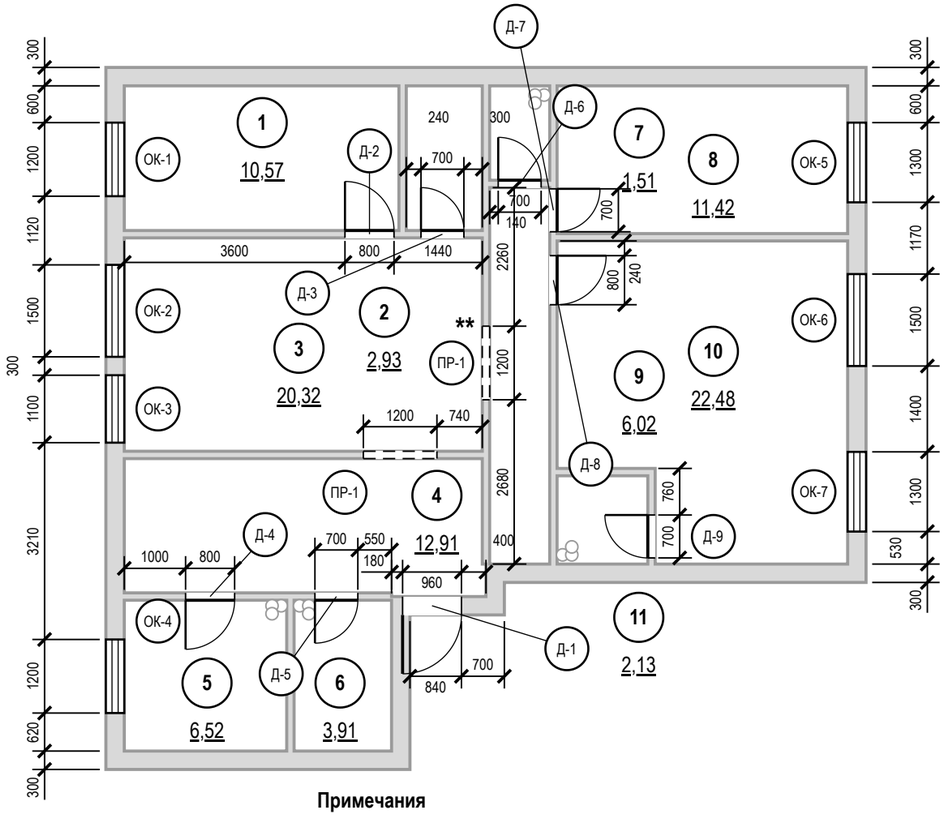

Условные обозначения

- стены (подложка обмера)
- дверь распашная, дуга открывания
- дверь скрытого монтажа
- дверь входная (полотно толще)
- портал (штрих — перемычка)
- оконный блок
- Д — марка типа (Д-N, ПР-N, ОК-N)
- 1 — номер помещения, площадь м²
- ** — «**» — предложение проектировщика, заказчиком не утверждено

Примечания

1. Размеры проёмов и привязки — в миллиметрах от чистых граней стен до отделки; привязка — от угла того помещения, со стороны которого стоит размер. Размер в ведомости — ширина × высота проёма от чистого пола 0,000. Откос от угла помещения до проёма с коробкой — не менее 50 мм.
2. Марки в кружках — типы заполнения проёмов (ГОСТ 21.501-2018, п. 5.3.2); одна марка — один типоразмер; количество сверено с планом.
3. Открывание: Л — петли слева, П — справа, если смотреть со стороны, куда открывается полотно (на себя).
4. Остекление окон: ОК-1 (пом. 1) — триплекс; ОК-2 (пом. 3) — триплекс; ОК-3 (пом. 3) — триплекс; ОК-4 (пом. 5) — триплекс; ОК-5 (пом. 8) — триплекс; ОК-6 (пом. 10) — триплекс; ОК-7 (пом. 10) триплекс. Тип стекла указать при заказе оконных блоков; замена на другое стекло — только по согласованию с автором проекта.
5. ОК-1, ОК-2, ОК-3, ОК-4, ОК-5, ОК-6, ОК-7: низ остекления 720 и 735 и 763 и 783 и 825 мм — ниже 900 мм от чистого пола, поэтому окно заказывать с безопасным стеклом (триплекс); ограждение проёма в проекте не задано (СП 54.13330.2022, п. 6.4.9; ГОСТ Р 56926).
6. Скрытые двери (Д-2…Д-9): проём замерить в чистоте; блок заказать до штукатурки (≈ 30 дн.), короб ставить до штукатурки; полотно навесить после чистовой отделки, красить в цвет стен. Порядок практика монтажа, изготовитель подтверждает.
7. Размер в ведомости — проёма: полотно скрытой двери уже проёма на коробку и зазор 10–15 мм (модель не выбрана); Д-2…Д-9 — существующие проёмы, до техзаключения не расширять.
8. Д-1: дуга наружу — по плану заказчика, не проверено; блок оставить или заменить — не решено.
9. Размеры проёмов и привязки сняты со скана плана заказчика и на объекте не замерены (обмерный план — лист 12).
10. Экспликация помещений — лист 12; в марках помещений — номер и площадь, м².
11. Привязка проёма к углу помещения меньше 1 мм на листе, размер на плане не показан: Д-7 — 30 мм; Д-9 — 100 мм.

1000 мм · печать 1:1

Ведомость заполнения проёмов

Марка	Наименование, обозначение	Проём ш×в, мм	Кол.	Откр.	Отделка полотна	Фурнитура	Прим.
Д-1	Блок дверной входной, ГОСТ 31173-2016	960×2100	1	Л	в комплекте блока	в комплекте блока (замки, глазок)	наружу
Д-2	Дверь скрытого монтажа, ТУ изготовителя	800×2100	1	П	окраска No. 291 с двух сторон	скрытые петли 3D, магнитный замок	
Д-3	Дверь скрытого монтажа, ТУ изготовителя	700×2100	1	П	S 0502-Y — пом. 2, No. 291 — пом. 3	скрытые петли 3D, магнитный замок	
Д-4	Дверь скрытого монтажа, ТУ изготовителя	800×2100	1	Л	окраска No. 291 с двух сторон	скрытые петли 3D, магнитный замок	
Д-5	Дверь скрытого монтажа, ТУ изготовителя	700×2100	1	Л	в тон облицовки — пом. 6, No. 291 — пом. 4	скрытые петли 3D, магнитный замок, фиксатор WC	порог 15
Д-6	Дверь скрытого монтажа, ТУ изготовителя	700×2100	1	П	S 0502-Y — пом. 7, No. 291 — пом. 9	скрытые петли 3D, магнитный замок	
Д-7	Дверь скрытого монтажа, ТУ изготовителя	700×2100	1	П	окраска No. 291 с двух сторон	скрытые петли 3D, магнитный замок	
Д-8	Дверь скрытого монтажа, ТУ изготовителя	800×2100	1	П	окраска No. 291 с двух сторон	скрытые петли 3D, магнитный замок	
Д-9	Дверь скрытого монтажа, ТУ изготовителя	700×2100	1	Л	в тон облицовки — пом. 11, No. 291 — пом. 10	скрытые петли 3D, магнитный замок, фиксатор WC	порог 15
ПР-1	Портал без заполнения	1200×2100	2				** пом. 3; б/п
ОК-1	Блок оконный, ГОСТ 23166-2021; стекло — триплекс	1200×1560	1				низ 720
ОК-2	Блок оконный, ГОСТ 23166-2021; стекло — триплекс	1500×1550	1				низ 735
ОК-3	Блок оконный, ГОСТ 23166-2021; стекло — триплекс	1100×1550	1				низ 735
ОК-4	Блок оконный, ГОСТ 23166-2021; стекло — триплекс	1200×1550	1				низ 763
ОК-5	Блок оконный, ГОСТ 23166-2021; стекло — триплекс	1300×1552	1				низ 783
ОК-6	Блок оконный, ГОСТ 23166-2021; стекло — триплекс	1500×1548	1				низ 825
ОК-7	Блок оконный, ГОСТ 23166-2021; стекло — триплекс	1300×1548	1				низ 825

Допущения и предложения на листе

Основа листа: размеры сняты со скана обмерного плана KV design (см): часть подписей не читается, помещения выровнены по читаемым размерам; контрольный обмер не выполнен (К-1); высота потолка 2650 мм принята по отметкам обмера (Н = 2,50…2,66 м, ригель 2,28 м) — уточнить при обмере (К-2); толщины стен 300 / 120 мм приняты, межквартирная стена и колонны — по скану, не замерены (К-1); разрешённая мощность 15 кВт принята по типовым ТУ; при объединении двух квартир — переоформление ТУ (К-4).
Знак «**» — предложение проектировщика, заказчиком не утверждено (согласовать с заказчиком): К-5: дверь пом. 3 (стена Б) — проём в межквартирной стене — объединение квартир, предложение до техзаключения.
См. лист открытых вопросов (лист 6, записи К-1, К-2, К-4, К-5).

Изм.	Кол.уч	Лист	№ док.	Подп.	Дата	ГД-2026-009-АИ			
						Квартира 103 м²			
						Общая площадь 100,72* м² · * размеры со скана, не замерены (реестр — л. 6, К-1)			
Разраб.		Кырлан А.С.			18.10.26	Дизайн-проект интерьера	Стадия	Лист	Листов
Пров.							РП	14	96
ГИП									
						План дверей и ведомость заполнения проёмов	Кырлан Александр Сергеевич		
Н. контр.									
Утв.						М 1:100			

выпуск 18.10.2026 № 53dc234b8d · стр. 17 из 135

02

Планировочное решение

Кырлан Александр Сергеевич

выпуск 18.10.2026 № 53dc234b8d · стр. 18 из 135

Концепция интерьера

Мид-сенчури · схема комплементарная · 60/30/10 · материалы, образы и зонирование

Идея

Стиль — мид-сенчури: оптимизм, функциональность, тёплое дерево, лёгкость, ретро без китча, связь с улицей, графичные акценты. Mid-century 65 % + ар-деко (art-deco.json) 35 %. Стены — School House White No. 291 и кремовый S 1005-Y20R, потолки — белый S 0502-Y; второй план — орех и тик, оливковый Bancha No. 298, сине-серый Inchyra Blue No. 289; акценты — горчица S 2050-Y20R, терракота S 3050-Y70R, тил S 5030-B10G, изумрудный бархат S 5040-B90G; металл — латунь. Мебель — авторские модели середины века (как предложение, модели уточняются с заказчиком). Цветовая схема — комплементарная, пропорция 60/30/10: база на стенах и потолках, вторичный цвет — в текстиле и мягкой мебели, акцент — точечно.

Мудборд: материалы и фактуры

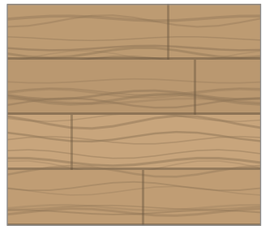

1167-4250
пол

A8UZ
пол, стены

Белый с лёгкой желтизной · NCS S 0502-Y
потолок, стены, плинтус

School House White — тёплый меловой белый · Farrow & Ball No. 291
стены, плинтус, потолок

Inchyra Blue — тёмный сине-серый · Farrow & Ball No. 289
акцент (стена А)

Tanner's Brown — тёмный шоколад · Farrow & Ball No. 255
акцент (стена А)

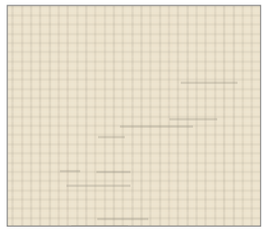

Лён, NCS S 1005-Y20R
портьеры-волна, Портьеры-волна

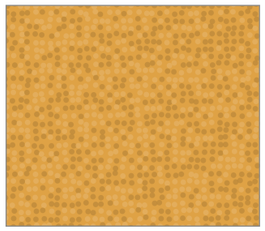

Шерсть, NCS S 2050-Y20R
ковёр под рабочей зоной, ковёр под кроватью

Бархат, Farrow & Ball No. 255
Подушки декоративные на диван

Палитра 60/30/10

60 % база — Farrow & Ball No. 291 School House White — тёплый меловой белый, LRV 73; NCS S 1005-Y20R Светлый кремовый, LRV 77; NCS S 0502-Y Белый с лёгкой желтизной, LRV 95

30 % вторичный — Farrow & Ball No. 298 Bancha — оливковый середины века, LRV 14; Farrow & Ball No. 289 Inchyra Blue — тёмный сине-серый, LRV 13; Farrow & Ball No. 255 Tanner's Brown — тёмный шоколад, LRV 7

10 % акцент — NCS S 2050-Y20R Горчичный, LRV 42; NCS S 3050-Y70R Терракотовый / жжёный оранжевый, LRV 18; NCS S 5030-B10G Тил, LRV 12; NCS S 5040-B90G Изумрудный, LRV 8

Функциональное зонирование (М 1:200)

- дневная зона: гостиная, кухня, столовая
- ночная зона: спальни
- мокрая зона: санузлы
- хранение: гардеробная, кладовая
- вход и коммуникации
- функциональная зона в помещении
- (1) номер помещения (лист 16)

Образы помещений

3. Гостиная-столовая — 20,32 м²
стены Farrow & Ball No. 291; акцент No. 255 на стене А

5. Кухня — 6,52 м²
стены Farrow & Ball No. 291
пол — 1167-4250

8. Спальня 2 — 11,42 м²
стены Farrow & Ball No. 291; акцент No. 289 на стене А

10. Спальня мастер — 22,48 м²
стены Farrow & Ball No. 291; акцент No. 289 на стене А

1. Кабинет-библиотека — 10,57 м²
стены Farrow & Ball No. 291; акцент No. 289 на стене А

4. Прихожая-холл — 12,91 м²
стены Farrow & Ball No. 291
пол — A8UZ

9. Коридор — 6,02 м²
стены Farrow & Ball No. 291
пол — 1167-4250

7. Постирочная — 1,51 м²
стены NCS S 0502-Y
пол — 1167-4250

6. Ванная — 3,91 м²
стены Atlas Concorde A8UZ
пол — A8UZ

11. Ванная мастер — 2,13 м²
стены Atlas Concorde A8UZ
пол — A8UZ

2. Кладовая — 2,93 м²
стены NCS S 0502-Y
пол — 1167-4250

Материалы и отделка

1167-4250
пол — пом. 1, 2, 3, 5, 7, 8, 9, 10

A8UZ
пол, стены — пом. 4, 6, 11

Керамогранит матовый
тон F497; 600×600
фартук — пом. 5

Farrow & Ball No. 291 School House White — тёплый меловой белый, LRV 73
Farrow & Ball Modern Emulsion, матовая
стены, плинтус, потолок — пом. 1, 3, 4, 5, 8, 9, 10

NCS S 0502-Y Белый с лёгкой желтизной, LRV 95
Tikkurila Anti-Reflex 2, глубокоматовая
потолок, стены, плинтус — пом. 1, 2, 4, 6, 7, 8, 9, 10, 11

Farrow & Ball No. 289 Inchyra Blue — тёмный сине-серый, LRV 13
акцентная стена
акцент (стена А) — пом. 1, 8, 10

Farrow & Ball No. 255 Tanner's Brown — тёмный шоколад, LRV 7
акцентная стена
акцент (стена А) — пом. 3

Текстиль и металл

Лён, NCS S 1005-Y20R
портьеры-волна, Портьеры-волна

Вуаль, NCS S 0502-Y
тюль

Шерсть, NCS S 2050-Y20R
ковёр под рабочей зоной, ковёр под кроватью

Букле, NCS S 3050-Y70R
подушки декоративные на кровать

Шерсть, Farrow & Ball No. 289
плед на кровать

Вуаль, Farrow & Ball No. 291
Тюль-вуаль

Шерсть, Farrow & Ball No. 298
ковёр мягкой группы, ковёр под кроватью

Бархат, Farrow & Ball No. 255
Подушки декоративные на диван

Шерсть, Farrow & Ball No. 255
Плед на диван

Чёрный матовый металл
зеркало, зеркало в рост

Чего избегаем

1) Ретро-парк: все акценты сразу (оранжевый + бирюза + горчица + атомные обои) — это тематический кафе-интерьер
2) Дешёвые реплики с неправильными пропорциями (толстые прямые ножки, утяжелённые спинки)
3) Холодный серо-белый сканди с ламинатом под беленый дуб — у мид-сенчури тёплое тёмное дерево
4) Лепнина, многоуровневые потолки, глянец и тяжёлые шторы с ламбрекенами
5) Сплошной тик: дерево на полу, стенах, мебели и потолке одного тона — нужен контраст светлых стен
6) Только винтаж без современной эргономики (кухни, хранение) — стиль ценил функциональность

Допущения и предложения на листе

Основа листа: размеры сняты со скана обмерного плана KV design (см): часть подписей не читается, помещения выровнены по читаемым размерам; контрольный обмер не выполнен (К-1); высота потолка 2650 мм принята по отметкам обмера (Н = 2,50…2,66 м, ригель 2,28 м) — уточнить при обмере (К-2); толщины стен 300 / 120 мм приняты, межквартирная стена и колонны — по скану, не замерены (К-1); разрешённая мощность 15 кВт принята по типовым ТУ; при объединении двух квартир — переоформление ТУ (К-4).
См. лист открытых вопросов (лист 6, записи К-1, К-2, К-4).

Примечания

1. Коды цвета — по веерам производителей (колерная карта, лист 42); перед закупкой краски — выкрас на стене объекта под дневным светом и лампами проекта.
2. Материалы — по ведомости отделки (лист 40); мебель, текстиль и декор — по спецификации (лист 17). Образцы доски, керамогранита и тканей утвердить до заказа.
3. Фактуры на листе условные, цвет передан по HEX-значениям производителей: при печати возможны отклонения, решение — только по физическому образцу.

						ГД-2026-009-АИ	
						Квартира 103 м²	
						Общая площадь 100,72* м² · * размеры со скана, не замерены (реестр — л. 6, К-1)	
Изм.	Кол.уч	Лист	№ док.	Подп.	Дата	Дизайн-проект интерьера	Стадия: РП · Лист: 15 · Листов: 96
Разраб.		Кырлан А.С.			18.10.26	Концепция интерьера М б/м	Кырлан Александр Сергеевич
Пров.							
ГИП							
Н. контр.							
Утв.							

выпуск 18.10.2026 № 53dc234b8d · стр. 19 из 135

План расстановки мебели

Мебель и оборудование · размеры в мм от чистовых стен · марки — по ведомости

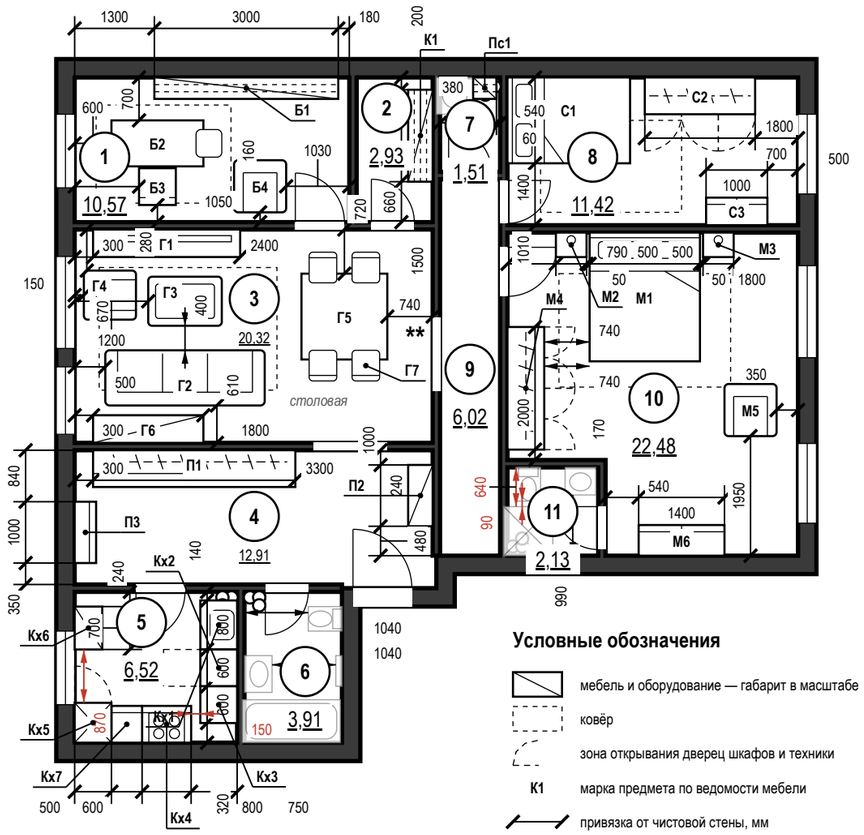

Условные обозначения

- мебель и оборудование — габарит в масштабе
- ковёр
- зона открывания дверец шкафов и техники
- К1 — марка предмета по ведомости мебели
- привязка от чистовой стены, мм
- ширина прохода, зазор, мм
- проход меньше нормы — расстановку изменить
- сантехприборы — подложка (лист ВК)
- существующие стены (сечение)
- ** — «**» — предложение проектировщика, заказчиком не утверждено
- стояк: К1 — канализация, В1 — ХВС, Т3 — ГВС
- 1 — номер помещения, площадь м²
- *зона* — функциональная зона помещения

Экспликация помещений

лист 12 · на плане — номера в марках

Ведомость мебели и оборудования

Марка	Наименование	Ш×Г×В, мм	Пом.	Кол.
Б1	Стеллаж-библиотека из ореха на	3000×350×2400	1	1
Б2	Письменный стол-бюро середины века	750×1500×750	1	1
Б3	Стул рабочий с подлокотниками	600×600×800	1	1
Б4	Кресло-лаунж с оттоманкой	850×850×850	1	1
К1	Стеллаж для хранения	1500×400×2400	2	1
Г1	ТВ-консоль из ореха на	2400×450×550	3	1
Г2	Диван середины века	2600×900×780	3	1
Г3	Стол журнальный	1200×800×400	3	1
Г4	Кресло	800×850×1070	3	1
Г5	Стол обеденный на одной ножке	1400×1400×730	3	1
Г6	Буфет-сервант из ореха на	1800×450×750	3	1
П1	Шкаф-купе с фасадами из	3300×600×2600	4	1
П2	Банкетка	1000×400×450	4	1
П3	Консоль ар-деко	1000×350×800	4	1
Кх1	Модуль под мойку	800×600×900	5	1
Кх2	Посудомоечная машина встроенная	600×600×900	5	1
Кх3	Модуль с ящиками	600×600×900	5	1
Кх4	Модуль с варочной панелью	800×600×900	5	1
Кх7	Модуль с ящиками между	500×600×900	5	1
Кх5	Колонна с холодильником	600×650×2100	5	1
Кх6	Стол барный у окна	700×450×900	5	1
Пс1	Полки для хранения	380×350×2000	7	1
С1	Кровать 1400×2000	1400×2000×450	8	1
С2	Шкаф распашной	1800×600×2400	8	1
С3	Туалетный столик середины века	1000×450×750	8	1
М1	Кровать 1800×2100 с высоким	1800×2100×450	10	1
М2	Тумба прикроватная	500×400×550	10	1
М3	Тумба прикроватная	500×400×550	10	1
М4	Шкаф распашной	2000×600×2400	10	1
М5	Кресло-лаунж с оттоманкой	850×850×850	10	1
М6	Комод ар-деко	1400×500×800	10	1
Г7	Стул обеденный к столу Г5	450×500×820	3	4

Ш — вдоль стены (изголовья), Г — от стены (длина кровати)

Материалы, модели, допуск замены — лист 17

Примечания

1. Размеры даны в мм от чистовых поверхностей стен: слой штукатурки 20 мм по блоку и 5 мм шпаклёвки по ГКЛ учтён. Перед заказом встроенной мебели — контрольный обмер после штукатурки.
2. Привязки мебели — от стен и углов помещения, а не от другой мебели; ширина проходов и зазоров показана стрелками.
3. Розетки, выводы и выключатели под мебель — см. лист 20 «План розеток и электровыводов»; сантехприборы и выводы воды лист 30.
4. План расстановки не является документацией для изготовления мебели: изделия — по чертежам мебельщика; покупную мебель заменять только на изделия не больше габарита из спецификации (лист 17).
5. Встроенная мебель «стена в стену» — с зазором 10 мм с каждой стороны или с компенсаторами.
6. Стулья обеденной группы (Г7 — 4 шт.) показаны в рабочем положении, задвинутыми под столешницу на 150 мм.

Допущения и предложения на листе

Основа листа: размеры сняты со скана обмерного плана KV design (см): часть подписей не читается, помещения выровнены по читаемым размерам; контрольный обмер не выполнен (К-1); высота потолка 2650 мм принята по отметкам обмера (Н = 2,50…2,66 м, ригель 2,28 м) — уточнить при обмере (К-2); толщины стен 300 / 120 мм приняты, межквартирная стена и колонны — по скану, не замерены (К-1); разрешённая мощность 15 кВт принята по типовым ТУ; при объединении двух квартир — переоформление ТУ (К-4).

Знак «**» — предложение проектировщика, заказчиком не утверждено (согласовать с заказчиком): К-5: дверь пом. 3 (стена Б) — проём в межквартирной стене — объединение квартир, предложение до техзаключения.

Открытые вопросы и конфликты по листу: К-1.

См. лист открытых вопросов (лист 6, записи К-1, К-2, К-4, К-5).

1000 мм · печать 1:1

Изм.	Кол.уч	Лист	№ док.	Подп.	Дата
Разраб.		Кырлан А.С.			18.10.26
Пров.					
ГИП					
Н. контр.					
Утв.					

ГД-2026-009-АИ

Квартира 103 м²

Общая площадь 100,72* м² · * размеры со скана, не замерены (реестр — л. 6, К-1)

Дизайн-проект интерьера

Стадия	Лист	Листов
РП	16	96

План расстановки мебели

М 1:100

Кырлан Александр Сергеевич

выпуск 18.10.2026 № 53dc234b8d · стр. 20 из 135

Спецификация мебели и оборудования

ПРЕДВАРИТЕЛЬНО · не для производства работ · открыто пунктов: 4 (реестр — л. 6)

Форма 1 ГОСТ 21.110-2013 · позиции мебели — по плану расстановки

Поз.	Наименование и техническая характеристика	Тип, марка, обозначение документа, опросного листа	Код продукции	Поставщик	Ед. измерения	Кол.	Масса 1 ед., кг	Примечание
	Мебель встроенная и корпусная (изготовление по чертежам мебельщика)							
П1	Шкаф-купе с фасадами из ореха и латунными профилями; корпус ЛДСП, фасады — матовая эмаль в цвет стен (Farrow & Ball No. 291); Ш×Г×В 3300×600×2600 мм			изготовление на заказ	шт.	1		пом. 4
Кх1	Модуль под мойку, фасады — шпон ореха; корпус ЛДСП, фасады — матовая эмаль в тон стен; Ш×Г×В 800×600×900 мм			изготовление на заказ	шт.	1		пом. 5
Кх2	Посудомоечная машина встроенная; корпус ЛДСП, фасады — матовая эмаль в тон стен; Ш×Г×В 600×600×900 мм			изготовление на заказ	шт.	1		пом. 5
Кх3	Модуль с ящиками; корпус ЛДСП, фасады — матовая эмаль в тон стен; Ш×Г×В 600×600×900 мм			изготовление на заказ	шт.	1		пом. 5
Кх4	Модуль с варочной панелью (индукция) и духовым шкафом; корпус ЛДСП, фасады — матовая эмаль в тон стен; Ш×Г×В 800×600×900 мм			изготовление на заказ	шт.	1		пом. 5
Кх5	Колонна с холодильником, ретро-фасад цвета тил; корпус ЛДСП, фасады — матовая эмаль в тон стен; Ш×Г×В 600×650×2100 мм			изготовление на заказ	шт.	1		пом. 5
Кх7	Модуль с ящиками между колонной и плитой; корпус ЛДСП, фасады — матовая эмаль в тон стен; Ш×Г×В 500×600×900 мм			изготовление на заказ	шт.	1		пом. 5
С2	Шкаф распашной, орех, латунные ручки; корпус ЛДСП, фасады — матовая эмаль в цвет стен (Farrow & Ball No. 291); Ш×Г×В 1800×600×2400 мм			изготовление на заказ	шт.	1		пом. 8
М4	Шкаф распашной, фасады — орех с латунными вставками; корпус ЛДСП, фасады — матовая эмаль в цвет стен (Farrow & Ball No. 291); Ш×Г×В 2000×600×2400 мм			изготовление на заказ	шт.	1		пом. 10
	Мебель покупная							
Б1	Стеллаж-библиотека из ореха на всю стену, латунные полкодержатели; шпон, дуб натуральный, матовое масло; Ш×Г×В 3000×350×2400 мм			аналог по характеристикам	шт.	1		пом. 1; замена ≤ габарита
Б2	Письменный стол-бюро середины века, орех, конические ножки; шпон, дуб натуральный, матовое масло; Ш×Г×В 750×1500×750 мм			аналог по характеристикам	шт.	1		пом. 1; замена ≤ габарита
Б3	Стул рабочий с подлокотниками, гнутая фанера и кожа; обивка — ткань, цвет Farrow & Ball No. 298; каркас — дуб натуральный; Ш×Г×В 600×600×800 мм			аналог по характеристикам	шт.	1		пом. 1; замена ≤ габарита
Б4	Кресло-лаунж с оттоманкой (в духе Eames Lounge Chair), палисандровый шпон, чёрная кожа; обивка — ткань, цвет Farrow & Ball No. 298; Ш×Г×В 850×850×850 мм			аналог по характеристикам	шт.	1		пом. 1; замена ≤ габарита
К1	Стеллаж для хранения, орех; каркас и полки — ЛДСП, декор «дуб натуральный»; Ш×Г×В 1500×400×2400 мм			аналог по характеристикам	шт.	1		пом. 2; замена ≤ габарита
Г1	ТВ-консоль из ореха на конических ножках, ТВ на стене; шпон, дуб натуральный, матовое масло; Ш×Г×В 2400×450×550 мм			аналог по характеристикам	шт.	1		пом. 3; замена ≤ габарита
Г2	Диван середины века (в духе Florence Knoll), букле горчичного цвета, латунные опоры; обивка — ткань, цвет Farrow & Ball No. 298; Ш×Г×В 2600×900×780 мм			аналог по характеристикам	шт.	1		пом. 3; замена ≤ габарита
Г3	Стол журнальный (в духе Noguchi Coffee Table), орех и стекло; шпон, дуб натуральный, матовое масло; Ш×Г×В 1200×800×400 мм			аналог по характеристикам	шт.	1		пом. 3; замена ≤ габарита
Г4	Кресло (в духе Egg Chair), изумрудный бархат; обивка — ткань, цвет Farrow & Ball No. 298; Ш×Г×В 800×850×1070 мм			аналог по характеристикам	шт.	1		пом. 3; замена ≤ габарита
Г5	Стол обеденный на одной ножке (в духе Tulip Table), мрамор Calacatta, d 1400; шпон, дуб натуральный, матовое масло; Ш×Г×В 1400×1400×730 мм			аналог по характеристикам	шт.	1		пом. 3; замена ≤ габарита
Г6	Буфет-сервант из ореха на конических ножках, раздвижные двери; шпон, дуб натуральный, матовое масло; Ш×Г×В 1800×450×750 мм			аналог по характеристикам	шт.	1		пом. 3; замена ≤ габарита
Г7	Стул обеденный к столу Г5; обивка — ткань, цвет Farrow & Ball No. 298; каркас — дуб натуральный; Ш×Г×В 450×500×820 мм			аналог по характеристикам	шт.	4		пом. 3; замена ≤ габарита
П2	Банкетка, изумрудный бархат, латунные ножки; Ш×Г×В 1000×400×450 мм			аналог по характеристикам	шт.	1		пом. 4; замена ≤ габарита
П3	Консоль ар-деко, чёрный лак и латунь; шпон, дуб натуральный, матовое масло; Ш×Г×В 1000×350×800 мм			аналог по характеристикам	шт.	1		пом. 4; замена ≤ габарита
Кх6	Стол барный у окна, терраццо; Ш×Г×В 700×450×900 мм			аналог по характеристикам	шт.	1		пом. 5; замена ≤ габарита

Примечания

1. Позиции мебели совпадают с марками на плане расстановки (лист 16); размеры Ш×Г×В — Ш вдоль стены, Г от стены.
2. Встроенная и корпусная мебель изготавливается по чертежам мебельщика после контрольного обмера; графы «Тип, марка» и «Код продукции» для неё не заполняются (ГОСТ 21.110-2013).
3. Покупные изделия — аналог по характеристикам: заменять только на изделия не больше указанного габарита и того же материала и цвета.
4. Материал и цвет, не указанные в данных изделия, приняты по концепции (лист 15): тон дерева — по полу, обивка — по вторичному цвету палитры; образцы согласовать до заказа.
5. Масса 1 ед. для изделий до 25 кг не указывается. Техника — по монтажным схемам изготовителя; выводы — по листам ЭОМ и ВК.

Допущения и предложения на листе

Основа листа: размеры сняты со скана обмерного плана KV design (см): часть подписей не читается, помещения выровнены по читаемым размерам; контрольный обмер не выполнен (К-1); высота потолка 2650 мм принята по отметкам обмера (Н = 2,50…2,66 м, ригель 2,28 м) — уточнить при обмере (К-2); толщины стен 300 / 120 мм приняты, межквартирная стена и колонны — по скану, не замерены (К-1); разрешённая мощность 15 кВт принята по типовым ТУ; при объединении двух квартир — переоформление ТУ (К-4).
См. лист открытых вопросов (лист 6, записи К-1, К-2, К-4).

Изм.	Кол.уч	Лист	№ док.	Подп.	Дата
Разраб.		Кырлан А.С.			18.10.26
Пров.					
ГИП					
Н. контр.					
Утв.					

ГД-2026-009-АИ

Квартира 103 м²

Общая площадь 100,72* м² · * размеры со скана, не замерены (реестр — л. 6, К-1)

	Стадия	Лист	Листов
Дизайн-проект интерьера	РП	17	96

Спецификация мебели и оборудования

М б/м

Кырлан Александр Сергеевич

выпуск 18.10.2026 № 53dc234b8d · стр. 21 из 135

Спецификация мебели и оборудования (продолжение)

Форма 1 ГОСТ 21.110-2013 · позиции мебели — по плану расстановки

ПРЕДВАРИТЕЛЬНО · не для производства работ · открыто пунктов: 4 (реестр — л. 6)

Поз.	Наименование и техническая характеристика	Тип, марка, обозначение документа, опросного листа	Код продукции	Поставщик	Ед. измерения	Кол.	Масса 1 ед., кг	Примечание
Пс1	Полки для хранения; каркас и полки — ЛДСП, декор «дуб натуральный»; Ш×Г×В 380×350×2000 мм			аналог по характеристикам	шт.	1		пом. 7; замена ≤ габарита
С1	Кровать 1400×2000, изголовье с каннелюрами, бархат цвета тил; мягкое изголовье, обивка — ткань, цвет Farrow & Ball No. 298; Ш×Г×В 1400×2000×450 мм			аналог по характеристикам	шт.	1		пом. 8; замена ≤ габарита
С3	Туалетный столик середины века с круглым зеркалом; шпон, дуб натуральный, матовое масло; Ш×Г×В 1000×450×750 мм			аналог по характеристикам	шт.	1		пом. 8; замена ≤ габарита
М1	Кровать 1800×2100 с высоким изголовьем ар-деко, изумрудный бархат, латунный кант; мягкое изголовье, обивка ткань, цвет Farrow & Ball No. 298; Ш×Г×В 1800×2100×450 мм			аналог по характеристикам	шт.	1		пом. 10; замена ≤ габарита
М2, М3	Тумба прикроватная, орех и латунь; шпон, дуб натуральный, матовое масло; Ш×Г×В 500×400×550 мм			аналог по характеристикам	шт.	2		пом. 10; замена ≤ габарита
М5	Кресло-лаунж с оттоманкой (в духе Eames Lounge Chair), коньячная кожа; обивка — ткань, цвет Farrow & Ball No. 298; Ш×Г×В 850×850×850 мм			аналог по характеристикам	шт.	1		пом. 10; замена ≤ габарита
М6	Комод ар-деко, макассар и латунь; шпон, дуб натуральный, матовое масло; Ш×Г×В 1400×500×800 мм			аналог по характеристикам	шт.	1		пом. 10; замена ≤ габарита
	Техника встраиваемая и бытовая, светильники под розетки							
	Посудомоечная машина встраиваемая, в модуле Кх2; ниша 600 мм			аналог по характеристикам	шт.	1		пом. 5; по схеме изготовителя
	Варочная панель встраиваемая, электрическая, в модуле Кх4			аналог по характеристикам	шт.	1		пом. 5; по схеме изготовителя
	Духовой шкаф встраиваемый, в модуле Кх4			аналог по характеристикам	шт.	1		пом. 5; по схеме изготовителя
	Холодильник встраиваемый, в модуле Кх5			аналог по характеристикам	шт.	1		пом. 5; по схеме изготовителя
	Вытяжка встраиваемая, над модулем Кх1			аналог по характеристикам	шт.	1		пом. 5; вывод Р21** (ЭОМ)
	Стиральная машина			аналог по характеристикам	шт.	1		пом. 6; вывод Р7** (ЭОМ)
	Стиральная машина, место по листу ВК (Пс2); Ш×Г 600×600 мм			аналог по характеристикам	шт.	1		пом. 7; по схеме изготовителя
	Торшер, у поз. Г6; абажур — ткань или опаловое стекло; лампа 2700 K			аналог по характеристикам	шт.	1		пом. 3; розетка Р3 (ЭОМ)
	Торшер, у поз. М4; абажур — ткань или опаловое стекло; лампа 2700 K			аналог по характеристикам	шт.	1		пом. 10; розетка Р5 (ЭОМ)
	Текстиль							
Т7	Портьеры-волна; лён 100 %; цвет NCS S 1005-Y20R; карниз 1820 мм, высота 2610 мм, сборка 2			аналог по характеристикам	шт.	2		пом. 1
Т8	Тюль; полиэстер 100 %; цвет NCS S 0502-Y; карниз 1820 мм, высота 2610 мм, сборка 2,5			аналог по характеристикам	шт.	1		пом. 1
Т9	Ковёр под рабочей зоной, геометрия середины века; шерсть 100 %; цвет NCS S 2050-Y20R; 2200×1600 мм			аналог по характеристикам	шт.	1		пом. 1; с подложкой
Т10	Подушки декоративные на кровать; букле (шерсть 60 %, полиэстер 40 %); цвет NCS S 3050-Y70R			аналог по характеристикам	шт.	3		пом. 1
Т12	Плед на кровать; шерсть мериноса 100 %; цвет Farrow & Ball No. 289			аналог по характеристикам	шт.	1		пом. 1
Т1	Портьеры-волна, два полотна; лён 100 %; цвет NCS S 1005-Y20R; карниз 2150 мм, высота 2690 мм, сборка 2			аналог по характеристикам	шт.	2		пом. 3
Т2	Тюль-вуаль, одно полотно; полиэстер 100 %; цвет Farrow & Ball No. 291; карниз 2150 мм, высота 2690 мм, сборка 2,5			аналог по характеристикам	шт.	1		пом. 3
Т3	Ковёр мягкой группы, абстрактная геометрия середины века; шерсть 100 %; цвет Farrow & Ball No. 298; 2900×2000 мм			аналог по характеристикам	шт.	1		пом. 3; с подложкой
Т4	Подушки декоративные на диван; лён 100 %; цвет NCS S 1005-Y20R			аналог по характеристикам	шт.	3		пом. 3
Т5	Подушки декоративные на диван, акцент; хлопковый бархат 100 %; цвет Farrow & Ball No. 255			аналог по характеристикам	шт.	2		пом. 3

Допущения и предложения на листе

Основа листа: размеры сняты со скана обмерного плана KV design (см): часть подписей не читается, помещения выровнены по читаемым размерам; контрольный обмер не выполнен (К-1); высота потолка 2650 мм принята по отметкам обмера (Н = 2,50…2,66 м, ригель 2,28 м) — уточнить при обмере (К-2); толщины стен 300 / 120 мм приняты, межквартирная стена и колонны — по скану, не замерены (К-1); разрешённая мощность 15 кВт принята по типовым ТУ; при объединении двух квартир — переоформление ТУ (К-4).

Знак «**» — предложение проектировщика, заказчиком не утверждено (согласовать с заказчиком): записи в реестре нет: Р21 — высота 2200 мм выше нормы 1 м (ПУЭ 6.6.30) по назначению: питание вытяжки М25, розетка в модуле за съёмной панелью; Р7 — по образцу: Р7, Р8 и Р33 на высоте 1000 мм — верхний предел нормы (ПУЭ, п. 6.6.30, не выше 1 м); флаг решения снят.

См. лист открытых вопросов (лист 6, записи К-1, К-2, К-4).

Изм.	Кол.уч	Лист	№ док.	Подп.	Дата
Разраб.		Кырлан А.С.			18.10.26
Пров.					
ГИП					
Н. контр.					
Утв.					

ГД-2026-009-АИ

Квартира 103 м²

Общая площадь 100,72* м² · * размеры со скана, не замерены (реестр — л. 6, К-1)

Дизайн-проект интерьера

Стадия	Лист	Листов
РП	18	96

Спецификация мебели и оборудования (продолжение)

М б/м

Кырлан Александр Сергеевич

Спецификация мебели и оборудования (продолжение)

Форма 1 ГОСТ 21.110-2013 · позиции мебели — по плану расстановки

ПРЕДВАРИТЕЛЬНО · не для производства работ · открыто пунктов: 4 (реестр — л. 6)

Поз.	Наименование и техническая характеристика	Тип, марка, обозначение документа, опросного листа	Код продукции	Поставщик	Ед. измерения	Кол.	Масса 1 ед., кг	Примечание
Т6	Плед на диван; шерсть мериноса 100 %; цвет Farrow & Ball No. 255			аналог по характеристикам	шт.	1		пом. 3
Т14	Рулонная штора кассетная, ткань димаут; полиэстер 100 %; цвет NCS S 1005-Y20R; карниз 890 мм, высота 1900 мм			аналог по характеристикам	шт.	1		пом. 5
Т11	Портьеры-волна; лён 100 %; цвет NCS S 1005-Y20R; карниз 1820 мм, высота 2610 мм, сборка 2			аналог по характеристикам	шт.	2		пом. 8
Т13	Тюль; полиэстер 100 %; цвет NCS S 0502-Y; карниз 1820 мм, высота 2610 мм, сборка 2,5			аналог по характеристикам	шт.	1		пом. 8
Т15	Ковёр под кроватью; шерсть 100 %; цвет NCS S 2050-Y20R; 2300×1500 мм			аналог по характеристикам	шт.	1		пом. 8; с подложкой
Т16	Подушки декоративные на кровать; букле (шерсть 60 %, полиэстер 40 %); цвет NCS S 3050-Y70R			аналог по характеристикам	шт.	3		пом. 8
Т17	Подушки на кровать, акцент; хлопковый бархат 100 %; цвет NCS S 5030-B10G			аналог по характеристикам	шт.	2		пом. 8
Т18	Плед на кровать; шерсть мериноса 100 %; цвет Farrow & Ball No. 289			аналог по характеристикам	шт.	1		пом. 8
Т19	Портьеры-волна; лён 100 %; цвет NCS S 1005-Y20R; карниз 2500 мм, высота 2610 мм, сборка 2			аналог по характеристикам	шт.	2		пом. 10
Т20	Тюль; полиэстер 100 %; цвет NCS S 0502-Y; карниз 2500 мм, высота 2610 мм, сборка 2,5			аналог по характеристикам	шт.	1		пом. 10
Т21	Ковёр под кроватью; шерсть 80 %, хлопок 20 %; цвет Farrow & Ball No. 298; 2800×1850 мм			аналог по характеристикам	шт.	1		пом. 10; с подложкой
Т22	Подушки декоративные на кровать; лён 100 %; цвет NCS S 1005-Y20R			аналог по характеристикам	шт.	3		пом. 10
Т23	Подушки на кровать, акцент; хлопковый бархат 100 %; цвет Farrow & Ball No. 289			аналог по характеристикам	шт.	2		пом. 10
Т24	Плед на кровать; шерсть мериноса 100 %; цвет Farrow & Ball No. 289			аналог по характеристикам	шт.	1		пом. 10
	Декор							
ДК3	Картина над креслом: графика середины века, рама — орех; 1000×700 мм; низ на 1100 мм от пола			аналог по характеристикам	шт.	1	4	пом. 1; крепление к стене
ДК1	Картина над буфетом: абстракция середины века, рама — латунь; 1200×900 мм; низ на 1000 мм от пола			аналог по характеристикам	шт.	1	6	пом. 3; крепление: планка на дюбелях, 4 точки
ДК2	Фикус лировидный в кашпо Ø400; 450×450 мм			аналог по характеристикам	шт.	1		пом. 3
ДК5	Зеркало; рама — чёрный матовый; 800×1800 мм; низ на 550 мм от пола			аналог по характеристикам	шт.	1	18	пом. 4; крепление: анкер, 4 шт.
ДК8	Часы настенные Ø400; 400×400 мм; центр на 1550 мм от пола			аналог по характеристикам	шт.	1	2	пом. 5; крепление: дюбель с крюком, 1 точка
ДК9	Хлорофитум хохлатый на подоконнике (отм. +0,800); 300×200 мм; низ на 800 мм от пола			аналог по характеристикам	шт.	1		пом. 5
ДК4	Картина над кроватью: графика в паспарту, рама — дуб; 1000×700 мм; низ на 1100 мм от пола			аналог по характеристикам	шт.	1	4	пом. 8; крепление к стене
ДК6	Зеркало в рост в тонкой чёрной раме; рама — чёрный матовый; 600×1600 мм; низ на 300 мм от пола			аналог по характеристикам	шт.	1	12	пом. 8; крепление: анкер для пустотелых оснований, 4 шт.
ДК7	Картина над кроватью: абстракция, холст, тонкая рама из дуба; 1200×700 мм; низ на 1300 мм от пола			аналог по характеристикам	шт.	1	4	пом. 10; крепление к стене

Допущения и предложения на листе

Основа листа: размеры сняты со скана обмерного плана KV design (см): часть подписей не читается, помещения выровнены по читаемым размерам; контрольный обмер не выполнен (К-1); высота потолка 2650 мм принята по отметкам обмера (Н = 2,50…2,66 м, ригель 2,28 м) — уточнить при обмере (К-2); толщины стен 300 / 120 мм приняты, межквартирная стена и колонны — по скану, не замерены (К-1); разрешённая мощность 15 кВт принята по типовым ТУ; при объединении двух квартир — переоформление ТУ (К-4).

См. лист открытых вопросов (лист 6, записи К-1, К-2, К-4).

Изм.	Кол.уч	Лист	№ док.	Подп.	Дата
Разраб.		Кырлан А.С.			18.10.26
Пров.					
ГИП					
Н. контр.					
Утв.					

ГД-2026-009-АИ

Квартира 103 м²

Общая площадь 100,72* м² · * размеры со скана, не замерены (реестр — л. 6, К-1)

Дизайн-проект интерьера

Стадия	Лист	Листов
РП	19	96

Спецификация мебели и оборудования (продолжение)

М б/м

Кырлан Александр Сергеевич

выпуск 18.10.2026 № 53dc234b8d · стр. 23 из 135

03

Электрооборудование

Кырлан Александр Сергеевич

выпуск 18.10.2026 № 53dc234b8d · стр. 24 из 135

План розеток и электровыводов

Розетки, выводы кабеля, щит · размеры в мм · высоты от чистого пола

ПРЕДВАРИТЕЛЬНО · не для производства работ · открыто пунктов: 4 (реестр — л. 6)

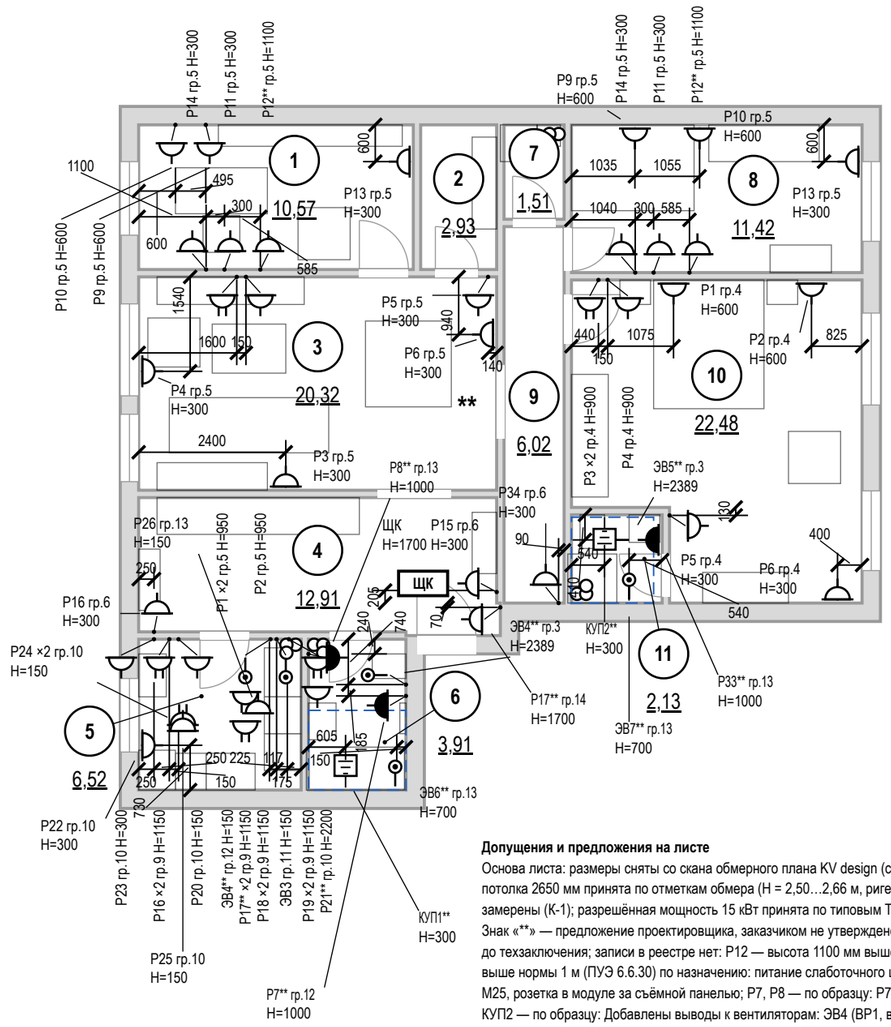

Условные обозначения

- розетка с заземляющим контактом; у знака — марка, ×N постов в рамке, гр. — группа щита, Н — высота оси, мм
- то же, рамка на 2 поста (число черточек — число постов)
- розетка влагозащищённая IP44
- вывод кабеля для подключения прибора (без розетки), марка ЭВ
- КУП — коробка уравнивания потенциалов (ДСУП), проводник к шине РЕ щита
- ЩК — щит квартирный
- знак разведён для читаемости: точка на стене — у выноски, привязка — до неё
- граница зоны 2 ванной (600 мм от ванны/поддона)
- мебель и сантехприборы — подложка
- стояк: К1 — канализация, В1 — ХВС, Т3 — ГВС
- (1) номер помещения, площадь м²

Допущения и предложения на листе

Основа листа: размеры сняты со скана обмерного плана KV design (см): часть подписей не читается, помещения выровнены по читаемым размерам; контрольный обмер не выполнен (К-1); высота потолка 2650 мм принята по отметкам обмера (Н = 2,50…2,66 м, ригель 2,28 м) — уточнить при обмере (К-2); толщины стен 300 / 120 мм приняты, межквартирная стена и колонны — по скану, не замерены (К-1); разрешённая мощность 15 кВт принята по типовым ТУ; при объединении двух квартир — переоформление ТУ (К-4).

Знак «**» — предложение проектировщика, заказчиком не утверждено (согласовать с заказчиком): К-5: дверь пом. 3 (стена Б) — проём в межквартирной стене — объединение квартир, предложение до техзаключения; записи в реестре нет: Р12 — высота 1100 мм выше нормы 1 м (ПУЭ 6.6.30) по назначению: питание ТВ над комодом, в одной зоне с выводами ТВ2 и LAN2; Р17 — высота 1700 мм выше нормы 1 м (ПУЭ 6.6.30) по назначению: питание слаботочного щита ЩС, рядом со щитом на его высоте; Р21 — высота 2200 мм выше нормы 1 м (ПУЭ 6.6.30) по назначению: питание вытяжки М25, розетка в модуле за съёмной панелью; Р7, Р8 — по образцу: Р7, Р8 и Р33 на высоте 1000 мм — верхний предел нормы (ПУЭ, п. 6.6.30, не выше 1 м); флаг решения снят; ЭВ4, КУП1, ЭВ5, КУП2 — по образцу: Добавлены выводы к вентиляторам: ЭВ4 (ВР1, ванная) и ЭВ5 (ВР3, санузел 2) — группа 3, высота 2389 мм, включение с основным светом, таймер выбега в вентиляторе; и коробки уравнивания потенциалов КУП1 (ванная) и КУП2 (санузел 2) — высота 300 мм, у входа, вне зон 0–2, проводник от шины РЕ щита ЩК, сече; ЭВ6, ЭВ7 — по образцу: Добавлены электрические полотенцесушители IP44: П10 в ванной (480 мм, низ 900 мм) и П13 в санузле 2 (400 мм, низ 900 мм), выводы ЭВ6 и ЭВ7; мощность группы 13 — 2,4 кВт вместо 1,8 кВт; Р33 — по образцу: Розетка Р33 на высоте 1100 мм, вне шва плитки.

Открытые вопросы и конфликты по листу: К-4.

См. лист открытых вопросов (лист 6, записи К-1, К-2, К-4, К-5).

Примечания

1. За отметку 0,000 принят уровень чистого пола. Высоты Н — от чистого пола до оси изделия; привязки — от чистовой грани стены до оси механизма (у рамки на несколько постов — до оси рамки).
2. Высота установки, не указанная на плане: розетки — 300 мм от чистого пола; выводы кабеля — по паспорту прибора.
3. Розетки в санузле — только вне зон 0–2 (ПУЭ 7.1.48, ГОСТ Р 50571.7.701-2024), IP44, через УЗО 30 мА.
4. Розеточные и мокрые линии — через УЗО или дифавтомат с током утечки не более 30 мА (ПУЭ 7.1.79); в санузле выполнить ДСУП (ПУЭ 7.1.87–7.1.88).
5. Кабель — медный, исполнение нг(А)-LS (ГОСТ 31565-2012); скрытая прокладка только горизонтально и вертикально, фактические трассы зафиксировать исполнительной схемой до закрытия отделкой.
6. Расчёт нагрузок, токов КЗ, селективности и сечений — по проекту ЭОМ организации с допуском СРО; лист задаёт состав, расположение и группы.
7. Выводы кухонной техники — после утверждения проекта кухни (ориентировочно); привязки выводов даны от осей модулей гарнитура и пересматриваются вместе с проектом кухни.
8. Электрический тёплый пол проектом не предусмотрен; при решении заказчика устроить — отдельный лист «План тёплых полов»: контуры с отступом 100 мм от стен и мебели без ножек, датчик в гофре, терморегулятор, своя группа щита через УЗО 30 мА.
9. Ведомости электроточек, изделий, светильников и расшифровка клавиш — лист 23.

1000 мм · печать 1:1

Изм.	Кол.уч	Лист	№ док.	Подп.	Дата
Разраб.		Кырлан А.С.			18.10.26
Пров.					
ГИП					
Н. контр.					
Утв.					

ГД-2026-009-АИ

Квартира 103 м²

Общая площадь 100,72* м² · * размеры со скана, не замерены (реестр — л. 6, К-1)

Дизайн-проект интерьера

Стадия	Лист	Листов
РП	20	96

План розеток и электровыводов

М 1:100

Кырлан Александр Сергеевич

выпуск 18.10.2026 № 53dc2348d8d · стр. 25 из 135

План освещения

Светильники, группы включения, извещатели · размеры в мм

ПРЕДВАРИТЕЛЬНО · не для производства работ · открыто пунктов: 4 (реестр — л. 6)

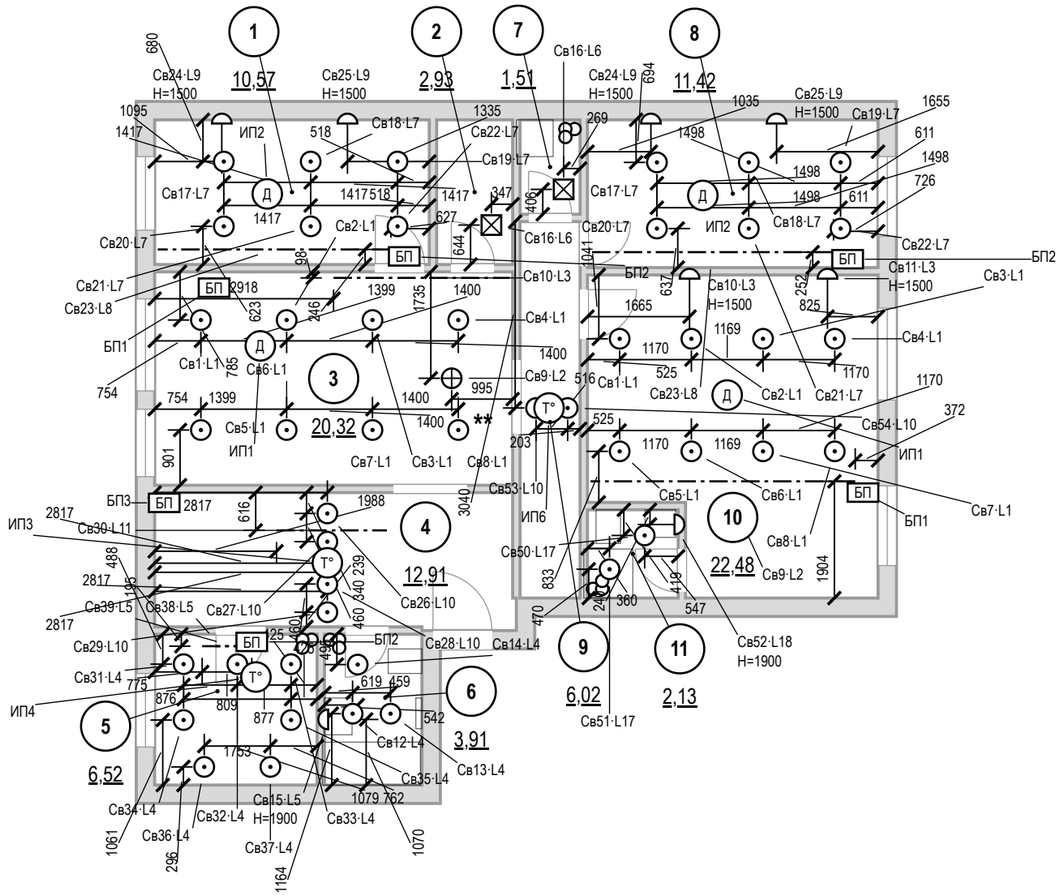

Условные обозначения

- светильник встраиваемый точечный
- светильник потолочный накладной
- светильник подвесной
- светильник настенный (бра), H — высота оси
- светодиодная лента в профиле / в карнизе короба
- Св1·L1 — марка светильника (как в ведомости и на развёртках) · группа включения L (лист выключателей)
- Д — извещатель пожарный дымовой автономный
- T° — извещатель пожарный тепловой
- БП — блок питания LED, с доступом (люк от 100×100 мм)
- 1 — номер помещения, площадь м²

Освещённость (оценка)

Пом.	S, м²	Ен, лк	Ф треб., лм	Ф по пр., лм
1	10,6	300	8930	6300
2	2,9	30	250	900
3	20,3	150	8590	8000
4	12,9	50	1820	2400
5	6,5	150	2750	7000
6	3,9	50	550	1500
7	1,5	75	320	900
8	11,4	150	4830	6300
9	6	50	850	1200
10	22,5	150	9500	8000
11	2,1	50	300	1100

Допущения и предложения на листе

Основа листа: размеры сняты со скана обмерного плана KV design (см): часть подписей не читается, помещения выровнены по читаемым размерам; контрольный обмер не выполнен (К-1); высота потолка 2650 мм принята по отметкам обмера (Н = 2,50…2,66 м, ригель 2,28 м) — уточнить при обмере (К-2); толщины стен 300 / 120 мм приняты, межквартирная стена и колонны — по скану, не замерены (К-1); разрешённая мощность 15 кВт принята по типовым ТУ; при объединении двух квартир — переоформление ТУ (К-4).

Знак «**» — предложение проектировщика, заказчиком не утверждено (согласовать с заказчиком): К-5: дверь пом. 3 (стена Б) — проём в межквартирной стене — объединение квартир, предложение до техзаключения.

См. лист открытых вопросов (лист 6, записи К-1, К-2, К-4, К-5).

Примечания

1. За отметку 0,000 принят уровень чистого пола. Высоты Н — от чистого пола до оси изделия; привязки — от чистовой грани стены до оси механизма (у рамки на несколько постов — до оси рамки).
2. Высота установки, не указанная на плане: светильники — на потолке; настенные — по отметке Н у знака. Привязки — до оси светильника от чистовой грани стены, по рядам.
3. Освещённость: Ен — СанПиН 1.2.3685-21, табл. 5.52 (на полу); Ф треб. = Ен·S/(U·MF) при U = 0,5 и MF = 0,71 (СП 52.13330.2016, табл. 4.3) — оценка, не светотехнический расчёт. Декоративная подсветка в Ф не входит.
4. Во влажных помещениях — светильники не ниже IP44; в зонах 0–2 ванной — по ГОСТ Р 50571.7.701-2024 (зона 1 — IPX5).
5. Розеточные и мокрые линии — через УЗО или дифавтомат с током утечки не более 30 мА (ПУЭ 7.1.79); в санузле выполнить ДСУП (ПУЭ 7.1.87–7.1.88).
6. Кабель — медный, исполнение нг(А)-LS (ГОСТ 31565-2012); скрытая прокладка только горизонтально и вертикально, фактические трассы зафиксировать исполнительной схемой до закрытия отделкой.
7. Расчёт нагрузок, токов КЗ, селективности и сечений — по проекту ЭОМ организации с допуском СРО; лист задаёт состав, расположение и группы.
8. Ведомость светильников — лист 23.

1000 мм · печать 1:1

Изм.	Кол.уч	Лист	№ док.	Подп.	Дата
Разраб.		Кырлан А.С.			18.10.26
Пров.					
ГИП					
Н. контр.					
Утв.					

ГД-2026-009-АИ

Квартира 103 м²

Общая площадь 100,72* м² · * размеры со скана, не замерены (реестр — л. 6, К-1)

Дизайн-проект интерьера

Стадия	Лист	Листов
РП	21	96

План освещения

М 1:100

Кырлан Александр Сергеевич

выпуск 18.10.2026 № 53dc234b8d · стр. 26 из 135

План выключателей и схема включения

Выключатели S, группы включения L, линии связи · размеры в мм

ПРЕДВАРИТЕЛЬНО · не для производства работ · открыто пунктов: 4 (реестр — л. 6)

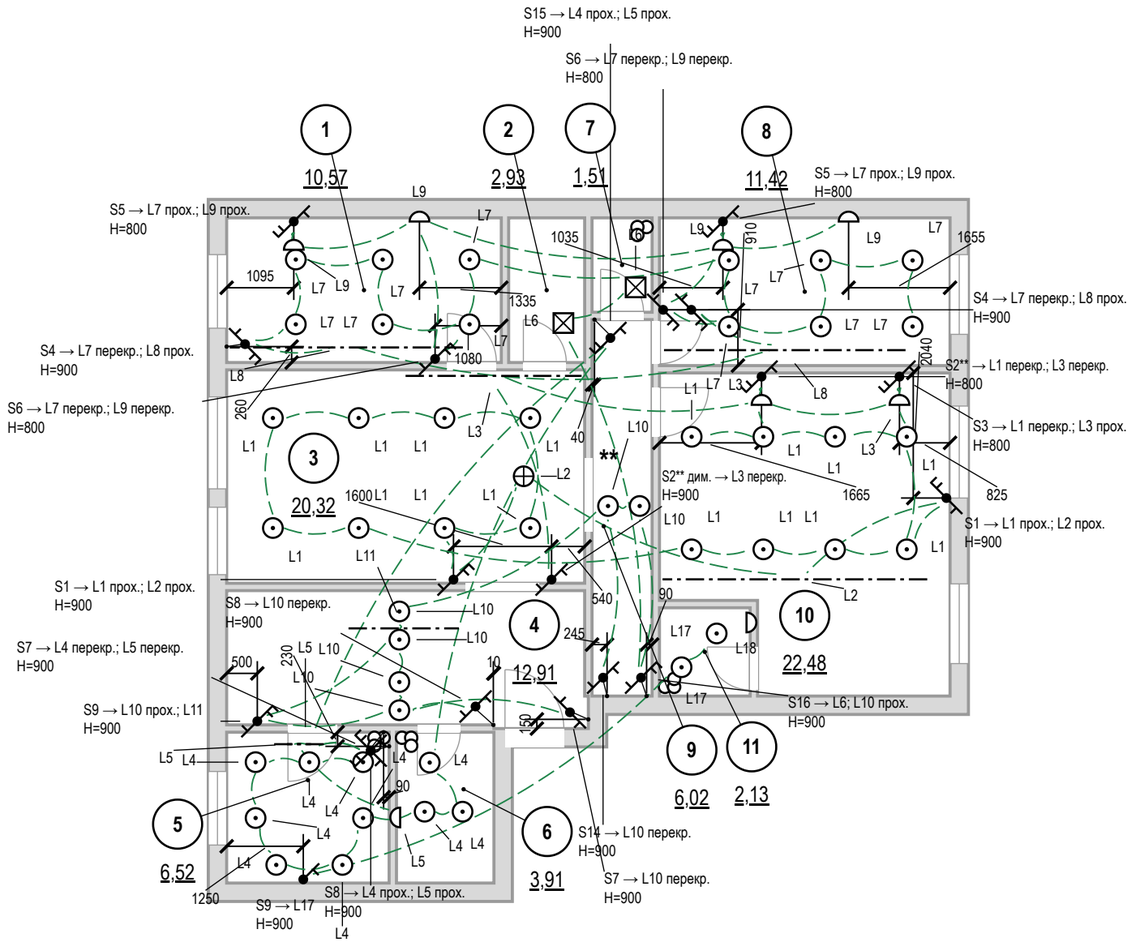

Условные обозначения

- выключатель одноклавишный
- выключатель с проходной или перекрёстной клавишей (обратный флажок); тип клавиши — в подписи
- S1 → — марка → группы по клавишам (через «;»): прох. — проходной, перекр. — перекрёстный, дим. — светорегулятор; H — высота
- линия связи: выключатель → светильники группы (не трасса кабеля)
- светильник встраиваемый точечный
- светильник потолочный накладной
- светильник подвесной
- светильник настенный (бра), H — высота оси
- светодиодная лента в профиле / в карнизе короба
- L1 — группа включения у светильника
- (1) — номер помещения, площадь м²

Допущения и предложения на листе

Основа листа: размеры сняты со скана обмерного плана KV design (см): часть подписей не читается, помещения выровнены по читаемым размерам; контрольный обмер не выполнен (К-1); высота потолка 2650 мм принята по отметкам обмера (H = 2,50…2,66 м, ригель 2,28 м) — уточнить при обмере (К-2); толщины стен 300 / 120 мм приняты, межквартирная стена и колонны — по скану, не замерены (К-1); разрешённая мощность 15 кВт принята по типовым ТУ; при объединении двух квартир — переоформление ТУ (К-4).

Знак «**» — предложение проектировщика, заказчиком не утверждено (согласовать с заказчиком): К-5: дверь пом. 3 (стена Б) — проём в межквартирной стене — объединение квартир, предложение до техзаключения; записи в реестре нет: S2 — светорегулятор добавлен под диммируемую ленту L3; уровни сценариев выбраны конвейером.

Примечания

См. лист открытых вопросов (лист 6, записи К-1, К-2, К-4, К-5).

1. За отметку 0,000 принят уровень чистого пола. Высоты H — от чистого пола до оси изделия; привязки — от чистовой грани стены до оси механизма (у рамки на несколько постов — до оси рамки).
2. Высота установки, не указанная на плане: выключатели — 900 мм от чистого пола, со стороны дверной ручки (ПУЭ 7.1.51).
3. Линии связи показывают, какой выключатель какую группу L включает; это не трасса кабеля. Трасса — принципиальная, фактическую зафиксировать исполнительной схемой.
4. Группы из нескольких мест (L7 — S4, S4, S5, S5, S6, S6; L8 — S4, S4; L9 — S5, S5, S6, S6; L1 — S1, S1, S2**, S3; L2 — S1, S1; L3 — S2**, S2**, S3; L10 — S7, S8, S9, S14, S16; L4 — S7, S8, S15; L5 — S7, S8, S15): на крайних местах — проходные клавиши, на промежуточных — перекрёстные; механизмы — в ведомости изделий.
5. Светорегулятор — по заднему фронту (для LED-драйверов), совместимость с драйверами проверить до закупки.
6. Розеточные и мокрые линии — через УЗО или дифавтомат с током утечки не более 30 мА (ПУЭ 7.1.79); в санузле выполнить ДСУП (ПУЭ 7.1.87–7.1.88).
7. Кабель — медный, исполнение нг(A)-LS (ГОСТ 31565-2012); скрытая прокладка только горизонтально и вертикально, фактические трассы зафиксировать исполнительной схемой до закрытия отделкой.
8. Расчёт нагрузок, токов КЗ, селективности и сечений — по проекту ЭОМ организации с допуском СРО; лист задаёт состав, расположение и группы.
9. Группы без выключателя: L18 — назначить управление до монтажа.
10. Расшифровка клавиш и ведомость изделий — лист 23.

1000 мм · печать 1:1

Изм.	Кол.уч	Лист	№ док.	Подп.	Дата
Разраб.		Кырлан А.С.			18.10.26
Пров.					
ГИП					
Н. контр.					
Утв.					

ГД-2026-009-АИ

Квартира 103 м²

Общая площадь 100,72* м² · * размеры со скана, не замерены (реестр — л. 6, К-1)

Дизайн-проект интерьера

Стадия	Лист	Листов
РП	22	96

План выключателей и схема включения

М 1:100

Кырлан Александр Сергеевич

выпуск 18.10.2026 № 53dc234b8d · стр. 27 из 135

Ведомость электроточек и изделий

Электроточки, изделия, светильники, клавиши выключателей · б/м

Ведомость электроточек

Марка	Пом.	Назначение	H, мм	Гр.
Р9	1	у кровати	600	5
Р10	1	у кровати	600	5
Р11	1	у комода	300	5
Р12**	1	ТВ над комодом (в одной зоне с ТВ2, LAN2)	1100	5
Р13	1	уборка	300	5
Р14	1	уборка у входа	300	5
Р1	3	ТВ-зона: телевизор, медиаплеер	950	5
Р2	3	ТВ-зона: саундбар	950	5
Р3	3	торшер у дивана М2	300	5
Р4	3	кресло у окна М4	300	5
Р5	3	обеденная зона, буфет М6	300	5
Р6	3	уборка	300	5
Р15	4	пылесос, сушилка обуви	300	6
Р16	4	уборка	300	6
Р17**	4	питание слаботочного щита (рядом с ЩС**)	1700	14
ЩК	4	щит квартирный ЩРВ-П-48	1700	
Р16	5	фартук: мелкая техника	1150	9
Р17**	5	фартук: мелкая техника	1150	9
Р18	5	фартук: мелкая техника	1150	9
Р19	5	фартук: мелкая техника	1150	9
Р20	5	холодильник встроенный М20 (розетка в модуле М21)	150	10
Р21**	5	вытяжка М25 (в модуле, съёмная панель)	2200	10
Р22	5	кухня: мелкая техника	300	10
Р23	5	уборка	300	10
Р24	5	торцевая панель острова М27: мелкая техника	150	10
Р25	5	торцевая панель острова М27: мелкая техника	150	10
Р26	5	посудомоечная машина в острове М27	150	13
ЭВ3	5	варочная панель М22	150	11
ЭВ4**	5	духовой шкаф М22 (вывод в соседнем модуле М23)	150	12

Ведомость электроточек (продолжение)

Марка	Пом.	Назначение	H, мм	Гр.
КУП1**	6	КУП — уравнивание потенциалов (ДСУП)	300	
Р7**	6	стиральная машина, IP44	1000	12
Р8**	6	фен у умывальника, IP44	1000	13
ЭВ4**	6	вентилятор ВР1 (таймер выбега)	2389	3
ЭВ6**	6	полотенцесушитель П10, IP44	700	13
Р9	8	у кровати	600	5
Р10	8	у кровати	600	5
Р11	8	у комода	300	5
Р12**	8	ТВ над комодом (в одной зоне с ТВ2, LAN2)	1100	5
Р13	8	уборка	300	5
Р14	8	уборка у входа	300	5
Р34	9	уборка	300	6
Р1	10	у кровати	600	4
Р2	10	у кровати	600	4
Р3	10	рабочий стол	900	4
Р4	10	рабочий стол	900	4
Р5	10	торшер у кресла	300	4
Р6	10	уборка	300	4
КУП2**	11	КУП — уравнивание потенциалов (ДСУП)	300	
Р33**	11	фен у умывальника, IP44	1000	13
ЭВ5**	11	вентилятор ВР3 (таймер выбега)	2389	3
ЭВ7**	11	полотенцесушитель П13, IP44	700	13

Ведомость изделий

Наименование	Марки	Ед.	Кол.
Розетка с з/к и защитными шторками, 16 А	по ведомости точек	шт	46
Розетка IP44 с крышкой, 16 А	Р7**, Р8**, Р33**	шт	3
Выключатель 1-клав.	S9	шт	1
Выключатель 1-клав. перекрёстный	S7, S8, S14	шт	3
Выключатель 2-клав. (перекрёстная + проходная)	S3, S4	шт	3
Выключатель 2-клав. (проходная + обычная)	S9, S16	шт	2

Ведомость изделий (продолжение)

Наименование	Марки	Ед.	Кол.
Выключатель 2-клав. перекрёстный	S2**, S6, S7	шт	4
Выключатель 2-клав. проходной	S1, S5, S8, S15	шт	6
Светорегулятор 1-канальный, задний фронт (LED)	S2**	шт	1
Датчик движения ночной подсветки	L11	шт	1
Рамка 1-постовая	в т. ч. 20 под выключ.	шт	55
Рамка 2-постовая		шт	7
Коробка установочная (подрозетник) Ø68	розетки, выключатели	шт	69
Вывод кабеля под прибор (клеммник)	ЭВ3, ЭВ4**, ЭВ5**, ЭВ6**, ЭВ7**	шт	6
Коробка уравнивания потенциалов КУП	КУП1**, КУП2**	шт	2
Блок питания LED 24 В, 200 Вт, дим.	БП1, БП2	шт	3
Блок питания LED 24 В, 100 Вт, дим.	БП1	шт	1
Блок питания LED 24 В, 20 Вт	БП3	шт	1
Блок питания LED 24 В, 30 Вт	БП2	шт	1
Извещатель дымовой автономный	ИП1, ИП2	шт	4
Извещатель тепловой	ИП3, ИП4, ИП6	шт	3
Щит квартирный (состав — лист щита)	ЩК	шт	1
Розетка компьютерная RJ45, кат. 6, с рамкой и подрозетником	LAN1, LAN2	шт	4
Розетка телевизионная (коаксиальная) с рамкой и подрозетником	ТВ1, ТВ2	шт	3
Точка доступа Wi-Fi (оборудование заказчика), питание PoE	АР1**	шт	1
Трубка или монитор домофона (поставка домофонной организации)	ДФ1	шт	1
Щит слаботочный ЩС**: корпус, DIN-рейка, розетки 220 В	ЩС**	шт	1
Патч-панель, портов не менее 5		шт	1
Коммутатор, портов не менее 5, из них PoE 1		шт	1

Ведомость изделий (продолжение)

Наименование	Марки	Ед.	Кол.
Кабель домофона — тип по системе поставщика (по лучам от ЩС**, запас 10 %)		м	4,3
Кабель коаксиальный RG-6 (75 Ом) к розеткам ТВ (по лучам от ЩС**, запас 10 %)		м	50,4
Кабель U/UTP кат. 6 (LAN, Wi-Fi и камеры по PoE) (по лучам от ЩС**, запас 10 %)		м	71,5

Ведомость светильников

Поз.	Марки	Тип	Кол.	P, Вт	Ф, лм	IP	Тц/Ra
1	Св17–Св22	встраиваемый точечный	12	12	1050		2700/90
2	Св23	светодиодная лента, 12,3 м	2	118,1	11070		2700/90
3	Св10, Св11, Св24, Св25	настенный (бра), H=1500	6	6	400		2700/90
4	Св16	потолочный накладной	2	10	900		3000/90
5	Св1–Св8, Св31–Св37	встраиваемый точечный	15	12	1000		3000/90
6	Св9	подвесной	1	15	1200		2700/90
7	Св10	светодиодная лента, 5 м	1	48	4500		2700/90
8	Св26–Св29, Св53, Св54	встраиваемый точечный	6	7	600		3000/90
9	Св30	светодиодная лента, 1,8 м	1	8,6	270		2700/90
10	Св38, Св39	линейный светильник	2	8	700		3000/90
11	Св12–Св14, Св51	встраиваемый точечный	4	6	500	44	3000/90
12	Св15, Св52	настенный (бра), H=1900	2	8	600	44	3000/90
13	Св1–Св8	встраиваемый точечный	8	12	1000		2700/90
14	Св9	светодиодная лента, 15,5 м	1	148,8	13950		2700/90
15	Св50	встраиваемый точечный	1	7	600	44	3000/90

Допущения и предложения на листе. Основа листа: размеры сняты со скана обмерного плана KV design (см): часть подписей не читается, помещения выровнены по читаемым размерам; контрольный обмер не выполнен (К-1); высота потолка 2650 мм принята по отметкам обмера (H = 2,50…2,66 м, ригель 2,28 м) — уточнить при обмере (К-2); толщины стен 300 / 120 мм приняты, межквартирная стена и колонны — по скану, не замерены (К-1); разрешённая мощность 15 кВт принята по типовым ТУ; при объединении двух квартир — переоформление ТУ (К-4). Знак «**» — предложено, не утверждено (согласовать): записи в реестре нет: Р12, S2, Р17, Р21, Р7, Р8, ЭВ4, КУП1, ЭВ6, Р33, ЭВ5, КУП2, ЭВ7, ЩС, АР1. См. лист открытых вопросов (лист 6, записи К-1, К-2, К-4).

Примечания

1. Ведомости сведены с планов розеток, освещения и выключателей; марки, группы и высоты — те же, что у знаков на планах.
2. Механизмы, рамки и светорегуляторы — одной серии; число постов и клавиш сверено с выбранной серией. Перекрёстная клавиша — отдельный механизм серии.
3. За отметку 0,000 принят уровень чистого пола. Высоты H — от чистого пола до оси изделия; привязки — от чистовой грани стены до оси механизма (у рамки на несколько постов — до оси рамки).
4. Розеточные и мокрые линии — через УЗО или дифавтомат с током утечки не более 30 мА (ПУЭ 7.1.79); в санузле выполнить ДСУП (ПУЭ 7.1.87–7.1.88).
5. Кабель — медный, исполнение нг(A)-LS (ГОСТ 31565-2012); скрытая прокладка только горизонтально и вертикально, фактические трассы зафиксировать исполнительной схемой до закрытия отделкой.
6. Расчёт нагрузок, токов КЗ, селективности и сечений — по проекту ЭОМ организации с допуском СРО; лист задаёт состав, расположение и группы.
7. Ведомости занимают 2 листов этого наименования: таблицы, не вошедшие в поле листа, продолжены на следующем листе.

Изм.	Кол.уч	Лист	№ док.	Подп.	Дата
Разраб.		Кырлан А.С.			18.10.26
Пров.					
ГИП					
Н. контр.					
Утв.					

ГД-2026-009-АИ

Квартира 103 м²

Общая площадь 100,72* м² · * размеры со скана, не замерены (реестр — л. 6, К-1)

Дизайн-проект интерьера

Стадия	Лист	Листов
РП	23	96

Ведомость электроточек и изделий

М б/м

Кырлан Александр Сергеевич

выпуск 18.10.2026 № 53dc234b8d · стр. 28 из 135

Ведомость электроточек и изделий (продолжение)

Электроточки, изделия, светильники, клавиши выключателей · б/м

Расшифровка клавиш

Марка	Пом.	Н, мм	Клав.	Механизм	Группа: светильники
S1	3	900	1	проходной	L1: Св1–Св8
			2	проходной	L2: Св9
S1	10	900	1	проходной	L1: Св1–Св8
			2	проходной	L2: Св9
S2**	3	900	1	светорегулятор	L3: Св10, Св11
S2**	10	800	1	перекрёстный	L1: Св1–Св8
			2	перекрёстный	L3: Св10, Св11
S3	10	800	1	перекрёстный	L1: Св1–Св8
			2	проходной	L3: Св10, Св11
S4	1	900	1	перекрёстный	L7: Св17–Св22
			2	проходной	L8: Св23
S4	8	900	1	перекрёстный	L7: Св17–Св22
			2	проходной	L8: Св23
S5	1	800	1	проходной	L7: Св17–Св22
			2	проходной	L9: Св24, Св25
S5	8	800	1	проходной	L7: Св17–Св22
			2	проходной	L9: Св24, Св25
S6	1	800	1	перекрёстный	L7: Св17–Св22
			2	перекрёстный	L9: Св24, Св25
S6	8	800	1	перекрёстный	L7: Св17–Св22
			2	перекрёстный	L9: Св24, Св25
S7	4	900	1	перекрёстный	L10: Св26–Св29, Св53, Св54
S7	5	900	1	перекрёстный	L4: Св12–Св14, Св31–Св37
			2	перекрёстный	L5: Св15, Св38, Св39
S8	4	900	1	перекрёстный	L10: Св26–Св29, Св53, Св54
S8	5	900	1	проходной	L4: Св12–Св14, Св31–Св37
			2	проходной	L5: Св15, Св38, Св39
S9	4	900	1	проходной	L10: Св26–Св29, Св53, Св54
			2	обычный	L11: Св30
S9	5	900	1	обычный	L17: Св50, Св51
S14	9	900	1	перекрёстный	L10: Св26–Св29, Св53, Св54

Расшифровка клавиш (продолжение)

Марка	Пом.	Н, мм	Клав.	Механизм	Группа: светильники
S15	9	900	1	проходной	L4: Св12–Св14, Св31–Св37
			2	проходной	L5: Св15, Св38, Св39
S16	9	900	1	обычный	L6: Св16
			2	проходной	L10: Св26–Св29, Св53, Св54

Допущения и предложения на листе

Основа листа: размеры сняты со скана обмерного плана KV design (см): часть подписей не читается, помещения выровнены по читаемым размерам; контрольный обмер не выполнен (К-1); высота потолка 2650 мм принята по отметкам обмера (Н = 2,50…2,66 м, ригель 2,28 м) — уточнить при обмере (К-2); толщины стен 300 / 120 мм приняты, межквартирная стена и колонны — по скану, не замерены (К-1); разрешённая мощность 15 кВт принята по типовым ТУ; при объединении двух квартир — переоформление ТУ (К-4).

Знак «**» — предложение проектировщика, заказчиком не утверждено (согласовать с заказчиком): записи в реестре нет: S2 — светорегулятор добавлен под диммируемую ленту L3; уровни сценариев выбраны конвейером.

См. лист открытых вопросов (лист 6, записи К-1, К-2, К-4).

Примечания

1. Продолжение ведомостей: лист 2 из 2 этого наименования; таблицы, прерванные на предыдущем листе, продолжены с заголовком «(продолжение)».
2. За отметку 0,000 принят уровень чистого пола. Высоты Н — от чистого пола до оси изделия; привязки — от чистовой грани стены до оси механизма (у рамки на несколько постов — до оси рамки).
3. Розеточные и мокрые линии — через УЗО или дифавтомат с током утечки не более 30 мА (ПУЭ 7.1.79); в санузле выполнить ДСУП (ПУЭ 7.1.87–7.1.88).
4. Кабель — медный, исполнение нг(А)-LS (ГОСТ 31565-2012); скрытая прокладка только горизонтально и вертикально, фактические трассы зафиксировать исполнительной схемой до закрытия отделкой.
5. Расчёт нагрузок, токов КЗ, селективности и сечений — по проекту ЭОМ организации с допуском СРО; лист задаёт состав, расположение и группы.

Изм.	Кол.уч	Лист	№ док.	Подп.	Дата
Разраб.		Кырлан А.С.			18.10.26
Пров.					
ГИП					
Н. контр.					
Утв.					

ГД-2026-009-АИ

Квартира 103 м²

Общая площадь 100,72* м² · * размеры со скана, не замерены (реестр — л. 6, К-1)

Дизайн-проект интерьера

Стадия	Лист	Листов
РП	24	96

Ведомость электроточек и изделий (продолжение)

М б/м

Кырлан Александр Сергеевич

Однолинейная схема щита

Щит квартирный ЩК · без масштаба

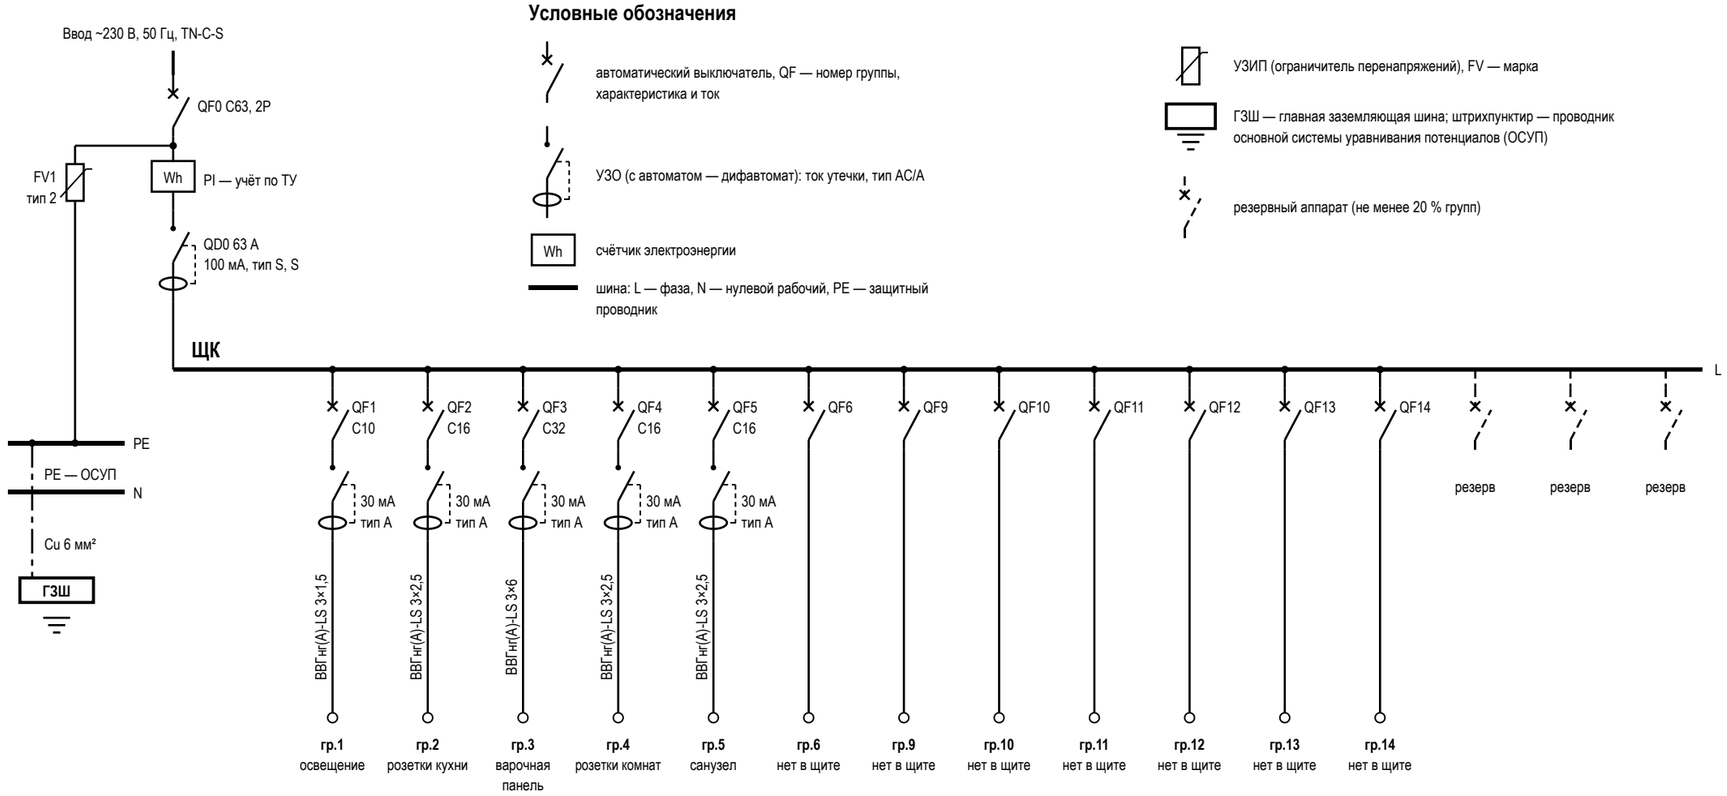

Условные обозначения

- автоматический выключатель, QF — номер группы, характеристика и ток
- УЗО (с автоматом — дифавтомат): ток утечки, тип AC/A
- Wh — счётчик электроэнергии
- шина: L — фаза, N — нулевой рабочий, PE — защитный проводник
- УЗИП (ограничитель перенапряжений), FV — марка
- ГЗШ — главная заземляющая шина; штрихпунктир — проводник основной системы уравнивания потенциалов (ОСУП)
- резервный аппарат (не менее 20 % групп)

Данные щитка

Показатель	Значение
Номер щитка	ЩК
Тип	ЩРВ-П-24, IP41
Уст. мощность, кВт	
Разреш. мощность, кВт	15
Расчётная, кВт	9,8
Автоматы 1п: занят. / рез.	5 / 3
Модулей: всего / занято	24 / 16
Ток на вводе, А	63
Вводной аппарат	QF0 C63, 2P
УЗИП	FV1, тип 2, ЩК, после счётчика
ГЗШ, проводник ОСУП	Cu 6 мм²

Таблица групп щита ЩК и кабельный журнал

№	Назначение	Помещения	Автомат	УЗО / дифавтомат	Кабель	Длина, м	Р, кВт	Точек
1	освещение	1, 2, 3, 5, 7, 8, 9, 10	C10	30 мА, тип A	ВВГнг(A)-LS 3×1,5	202,8		69
2	розетки кухни	4, 5, 9	C16	30 мА, тип A	ВВГнг(A)-LS 3×2,5	60,3		13
3	варочная панель	6, 9, 11	C32	30 мА, тип A	ВВГнг(A)-LS 3×6	42,6		10
4	розетки комнат	10	C16	30 мА, тип A	ВВГнг(A)-LS 3×2,5	36,6		6
5	санузел	1, 3, 8	C16	30 мА, тип A	ВВГнг(A)-LS 3×2,5	84,4		18
6	нет в щите	4, 9						3
9	нет в щите	5						4
10	нет в щите	5						6
11	нет в щите	5						1
12	нет в щите	5, 6						2
13	нет в щите	5, 6, 11						5
14	нет в щите	4						1
	Итого по сечениям ВВГнг(A)-LS, м: 3×1,5 — 202,8; 3×2,5 — 181,3; 3×6 — 42,6					426,7		

Примечания

1. Схема однолинейная: одна линия — фаза, N и PE группы; аппараты — в отключённом положении (ГОСТ 2.702, ГОСТ 2.755). Номера групп — как у точек на планах (гр.). За отметку 0,000 принят уровень чистого пола; высота щита — по плану розеток.
2. Розеточные и мокрые линии — через УЗО или дифавтомат с током утечки не более 30 мА (ПУЭ 7.1.79); в санузле выполнить ДСУП (ПУЭ 7.1.87–7.1.88).
3. УЗО тип A — для линий с электроникой, стиральной и посудомоечной машиной, LED-драйверами; тип AC — только для чисто активной нагрузки.
4. Кабель — медный, исполнение нг(A)-LS (ГОСТ 31565-2012); скрытая прокладка только горизонтально и вертикально, фактические трассы зафиксировать исполнительной схемой до закрытия отделкой.
5. Номинал автомата — не выше допустимого тока кабеля: 1,5 мм² — до 10 А, 2,5 мм² — до 16 А. Резерв щита — не менее 20 % модулей.
6. Расчёт нагрузок, токов КЗ, селективности и сечений — по проекту ЭОМ организации с допуском СРО; лист задаёт состав, расположение и группы.
7. УЗИП FV1 — после вводного автомата, проводник к шине PE — кратчайший, без петель. Шина PE щита соединяется с ГЗШ проводником ОСУП; к ГЗШ присоединяются трубы водопровода и отопления на вводе в квартиру (ПУЭ 7.1.87). Шины N и PE — раздельные, после разделения PEN не объединяются.
8. До подключения нагрузки — приёмо-сдаточные испытания с протоколом: сопротивление изоляции линий не менее 0,5 МОм, срабатывание УЗО по току и времени, непрерывность защитных проводников PE (ПУЭ, гл. 1.8).
9. Группы с пометкой «нет в щите» есть на планах, но не описаны в щите — дополнить аппаратами до закупки.

Допущения и предложения на листе

Основа листа: размеры сняты со скана обмерного плана KV design (см): часть подписей не читается, помещения выровнены по читаемым размерам; контрольный обмер не выполнен (К-1); высота потолка 2650 мм принята по отметкам обмера (Н = 2,50…2,66 м, ригель 2,28 м) — уточнить при обмере (К-2); толщины стен 300 / 120 мм приняты, межквартирная стена и колонны — по скану, не замерены (К-1); разрешённая мощность 15 кВт принята по типовым ТУ; при объединении двух квартир — переоформление ТУ (К-4).

Открытые вопросы и конфликты по листу: К-4.

См. лист открытых вопросов (лист 6, записи К-1, К-2, К-4).

Изм.	Кол.уч	Лист	№ док.	Подп.	Дата
Разраб.		Кырлан А.С.			18.10.26
Пров.					
ГИП					
Н. контр.					
Утв.					

ГД-2026-009-АИ

Квартира 103 м²

Общая площадь 100,72* м² · * размеры со скана, не замерены (реестр — л. 6, К-1)

Дизайн-проект интерьера

Стадия	Лист	Листов
РП	25	96

Однолинейная схема щита

М б/м

Кырлан Александр Сергеевич

выпуск 18.10.2026 № 53dc234b8d · стр. 30 из 135

План принципиальных трасс

Силовые трассы и объёмы электромонтажа, слаботочка в объёмах · размеры в мм

ПРЕДВАРИТЕЛЬНО · не для производства работ · открыто пунктов: 4 (реестр — л. 6)

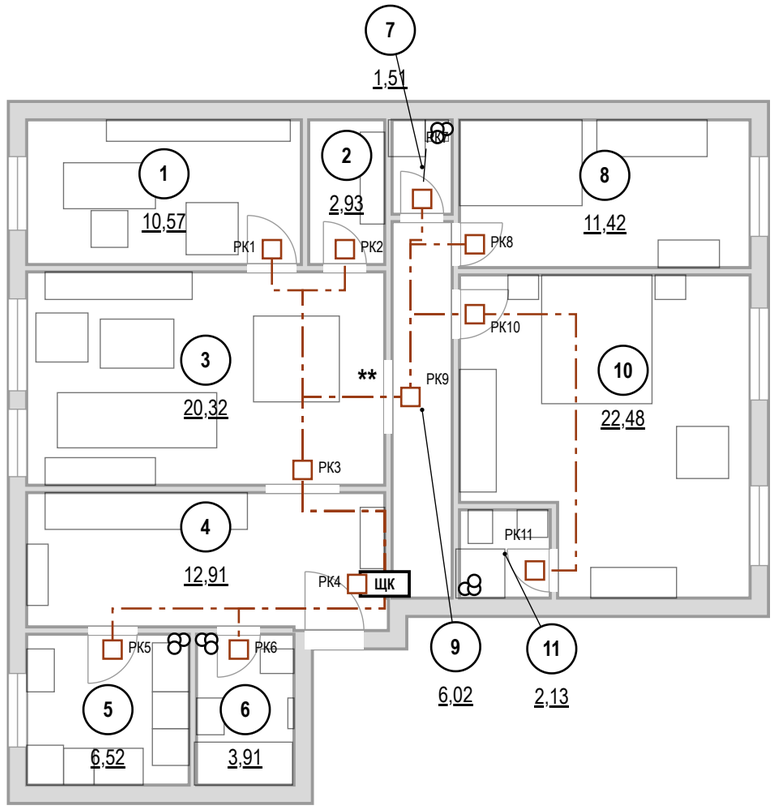

Кабель по группам ВВГнг(А)-LS, м

Гр.	мм²	Трасса	Данные
1	3×1,5	202,8	
2	3×2,5	60,3	
3	3×6	42,6	

Гр.	мм²	Трасса	Данные
4	3×2,5	36,6	
5	3×2,5	84,4	
Σ		**426,7**	

Экспликация помещений

№	Помещение	Площадь, м²
1	Кабинет-библиотека	10,57
2	Кладовая	2,93
3	Гостиная-столовая	20,32
4	Прихожая-холл	12,91
5	Кухня	6,52
6	Ванная	3,91
7	Постирочная	1,51
8	Спальня 2	11,42
9	Коридор	6,02
10	Спальня мастер	22,48
11	Ванная мастер	2,13
	Итого (общая площадь)	100,72

Объёмы прокладки

Работа, материал	Ед.	Кол.
Гофротруба Ø20 в потолочном пространстве	м	186,9
Кабель-канал плинтуса для силовых линий	м	106,1
Короб или накладной канал для вертикальных спусков и подъёмов	м	64,9
Коробка распределительная (РК) над дверью помещения	шт	11
Слаботочка: кабель домофона	м	4,3
Слаботочка: Кабель коаксиальный RG-6 (75 Ом) к розеткам ТВ	м	50,4
Слаботочка: U/UTP кат. 6 (LAN, Wi-Fi, камеры)	м	71,5
Слаботочка: гофротруба Ø20 отдельно от силовых	м	113,6

Штробы — только после заключения

Работа	Ед.	Кол.
Вертикальные штробы 20×20 мм от потолка до каждой настенной точки (в маршрут без штроб не входят)	м	134,73

Условные обозначения

- **ЩК** — щит квартирный
- РК — распределительная коробка над дверью помещения
- магистраль от щита к РК: потолочное пространство, гофра
- мебель и сантехприборы — подложка

Допущения и предложения на листе

Основа листа: размеры сняты со скана обмерного плана KV design (см): часть подписей не читается, помещения выровнены по читаемым размерам; контрольный обмер не выполнен (К-1); высота потолка 2650 мм принята по отметкам обмера (Н = 2,50…2,66 м, ригель 2,28 м) — уточнить при обмере (К-2); толщины стен 300 / 120 мм приняты, межквартирная стена и колонны — по скану, не замерены (К-1); разрешённая мощность 15 кВт принята по типовым ТУ; при объединении двух квартир — переоформление ТУ (К-4).

Знак «**» — предложение проектировщика, заказчиком не утверждено (согласовать с заказчиком): К-5: дверь пом. 3 (стена Б) — проём в межквартирной стене — объединение квартир, предложение до техзаключения; записи в реестре нет: ЩС — щит слаботочный: место и состав.

Примечания

См. лист открытых вопросов (лист 6, записи К-1, К-2, К-4, К-5).

1. За отметку 0,000 принят уровень чистого пола. Высоты Н — от чистого пола до оси изделия; привязки — от чистовой грани стены до оси механизма (у рамки на несколько постов — до оси рамки).
2. Розеточные и мокрые линии — через УЗО или дифавтомат с током утечки не более 30 мА (ПУЭ 7.1.79); в санузле выполнить ДСУП (ПУЭ 7.1.87–7.1.88).
3. Кабель — медный, исполнение нг(А)-LS (ГОСТ 31565-2012); скрытая прокладка только горизонтально и вертикально, фактические трассы зафиксировать исполнительной схемой до закрытия отделкой.
4. Расчёт нагрузок, токов КЗ, селективности и сечений — по проекту ЭОМ организации с допуском СРО; лист задаёт состав, расположение и группы.
5. Длины — по плану: от щита вверх в потолочное пространство, по дверям и коридору без захода в мокрые помещения к распределительной коробке над дверью, далее к точкам; вертикали считаются вниз и обратно (у последней точки цепочки — в один конец); запас 10 %. Трассы принципиальные: фактическую зафиксировать исполнительной схемой до закрытия отделкой.
6. Несущие стены не определены: штробы в стенах не выполнять. Маршрут проложен без штроб: горизонтали — за потолком в гофре (186,9 м) и в кабель-канале плинтуса (106,1 м), вертикали — в коробе или накладном канале (114,3 м кабеля). Точек: за потолком — 59, спуск из потолка — 13, по плинтусу — 12, плинтус и подъём 32.
7. Вариант со штробами — работа после технического заключения: 134,73 м вертикальных штроб от потолка до каждой настенной точки; условие — только после технического заключения: стена не несущая (или вертикальная штроба в несущей согласована конструктором), глубина и ширина 20–25 мм, не в зонах 0–2 ванной. Без заключения и согласования конструктора в смету и в график эта работа не входит.
8. Слаботочные сети: кабели и точки считаются по лучам от ЩС** (лист слаботочных сетей): 126 м, портов патч-панели и коммутатора не менее 5; из точек 1 предложения листа слаботочки, не подтверждённые заказчиком. Изделия — в ведомости изделий.

1000 мм · печать 1:1

Изм.	Кол.уч	Лист	№ док.	Подп.	Дата
Разраб.		Кырлан А.С.			18.10.26
Пров.					
ГИП					
Н. контр.					
Утв.					

ГД-2026-009-АИ

Квартира 103 м²

Общая площадь 100,72* м² · * размеры со скана, не замерены (реестр — л. 6, К-1)

Дизайн-проект интерьера

Стадия	Лист	Листов
РП	26	96

План принципиальных трасс

М 1:100

Кырлан Александр Сергеевич

выпуск 18.10.2026 № 53dc234b8d · стр. 31 из 135

План слаботочных сетей

Интернет, ТВ, домофон · размеры в мм · высоты от чистого пола

ПРЕДВАРИТЕЛЬНО · не для производства работ · открыто пунктов: 4 (реестр — л. 6)

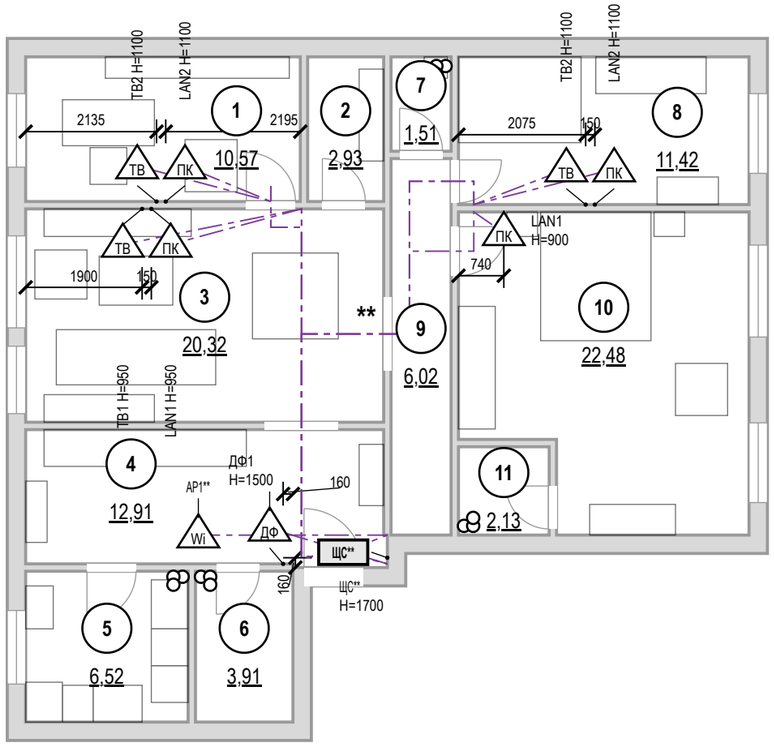

Ведомость слаботочных точек

Марка	Пом.	Назначение	H, мм	Кабель
TB2	1	розетка ТВ	1100	RG-6
LAN2	1	розетка LAN (RJ45)	1100	U/UTP кат. 6
TB1	3	розетка ТВ	950	коаксиальный RG-6
LAN1	3	розетка LAN (RJ45)	950	U/UTP кат. 6
ЩС**	4	щит слаботочный	1700	ввод пров.
ДФ1	4	домофон (трубка)	1500	по системе
AP1**	4	точка доступа Wi-Fi		U/UTP кат. 6
TB2	8	розетка ТВ	1100	RG-6
LAN2	8	розетка LAN (RJ45)	1100	U/UTP кат. 6
LAN1	10	розетка LAN (RJ45)	900	U/UTP кат. 6

Условные обозначения

- **ЩС** — щит слаботочный: ввод провайдера, роутер, коммутатор
- ПК — розетка компьютерная RJ45
- ТВ — розетка телевизионная
- ДФ — трубка или монитор домофона
- Wi — точка доступа Wi-Fi (питание PoE)
- кабель от ЩС до точки, отдельным лучом
- мебель и сантехприборы — подложка
- (1) — номер помещения, площадь м²

Допущения и предложения на листе

Основа листа: размеры сняты со скана обмерного плана KV design (см): часть подписей не читается, помещения выровнены по читаемым размерам; контрольный обмер не выполнен (К-1); высота потолка 2650 мм принята по отметкам обмера (Н = 2,50…2,66 м, ригель 2,28 м) — уточнить при обмере (К-2); толщины стен 300 / 120 мм приняты, межквартирная стена и колонны — по скану, не замерены (К-1); разрешённая мощность 15 кВт принята по типовым ТУ; при объединении двух квартир — переоформление ТУ (К-4).

Знак «**» — предложение проектировщика, заказчиком не утверждено (согласовать с заказчиком): К-5: дверь пом. 3 (стена Б) — проём в межквартирной стене — объединение квартир, предложение до техзаключения; записи в реестре нет: ЩС — щит слаботочный: место и состав; AP1 — точка доступа Wi-Fi: число и места.

См. лист открытых вопросов (лист 6, записи К-1, К-2, К-4, К-5).

Примечания

1. За отметку 0,000 принят уровень чистого пола. Высоты Н — от чистого пола до оси изделия; привязки — от чистовой грани стены до оси механизма (у рамки на несколько постов — до оси рамки).
2. Высота установки, не указанная на плане: розетки LAN и ТВ — 300 мм от чистого пола.
3. Слаботочные кабели — отдельно от силовых: в своей трубе или лотке, при параллельной прокладке не ближе 100 мм к силовым, пересечения под прямым углом; каждую точку — отдельным кабелем от ЩС** без скруток.
4. Трассы на листе — принципиальные; фактические зафиксировать исполнительной схемой до закрытия отделкой. Силовые линии, УЗО 30 мА, ДСУП, кабель нг(А)-LS — по листам розеток и щита.
5. Проект силовой части и расчёт токов КЗ — по проекту ЭОМ; слаботочная часть согласуется с провайдером и управляющей компанией (домофон, коллективное ТВ).

1000 мм · печать 1:1

Изм.	Кол.уч	Лист	№ док.	Подп.	Дата
Разраб.		Кырлан А.С.			18.10.26
Пров.					
ГИП					
Н. контр.					
Утв.					

ГД-2026-009-АИ

Квартира 103 м²

Общая площадь 100,72* м² · * размеры со скана, не замерены (реестр — л. 6, К-1)

Дизайн-проект интерьера

Стадия	Лист	Листов
РП	27	96

План слаботочных сетей

М 1:100

Кырлан Александр Сергеевич

выпуск 18.10.2026 № 53dc234b8d · стр. 32 из 135

04

Отопление и вентиляция

Кырлан Александр Сергеевич

выпуск 18.10.2026 53dc234b8d · стр. 33 из 135

План вентиляции

Вытяжка, приток, переток · кондиционирование не предусмотрено · размеры в мм · высоты от чистого пола

ПРЕДВАРИТЕЛЬНО · не для производства работ · открыто пунктов: 4 (реестр — л. 6)

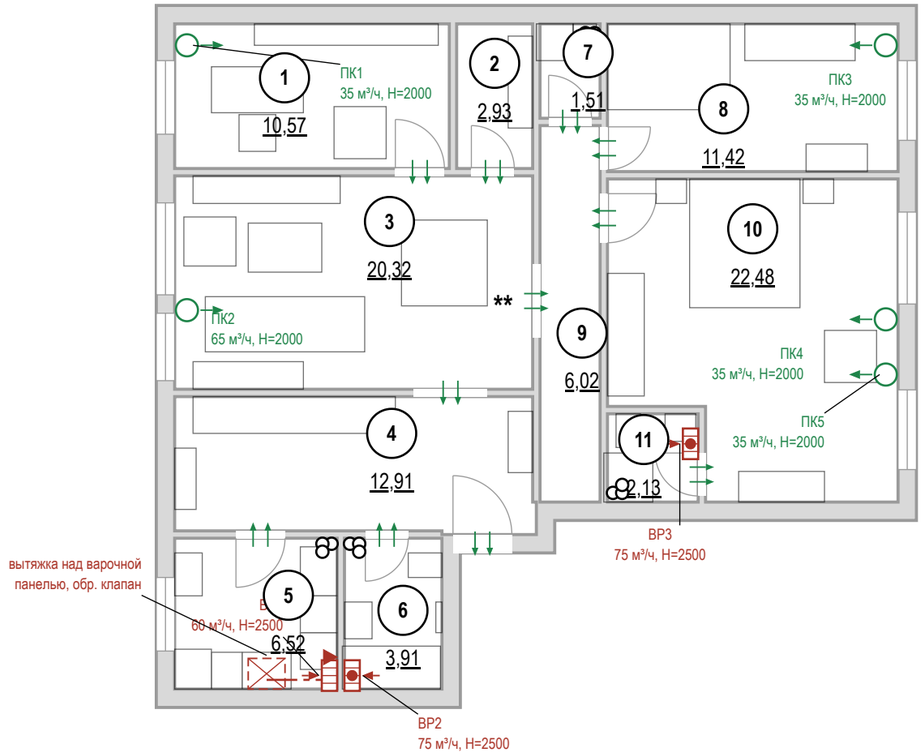

Условные обозначения

- стояк: К1 — канализация, В1 — ХВС, Т3 — ГВС
- 1 — номер помещения, площадь м²
- вытяжная решётка в вентканал: марка, расход м³/ч, Н центра от чистого пола
- вытяжная решётка с бытовым вентилятором и обратным клапаном: марка, расход, Н
- приточный клапан (КИВ) в наружной стене: марка, расход, Н центра
- переток: зазор под полотном или переточная решётка
- кухонная вытяжка над варочной панелью
- воздуховод кухонной вытяжки в коробе под потолком
- отдельный вход воздуховода в вентканал, обратный клапан
- ** — «**» — предложение проектировщика, заказчиком не утверждено

Воздухообмен, м³/ч

№	Помещение	Выт. норма	Выт. проект	Прит. норма	Прит. проект	Устройства
1	Кабинет-библиотека			32	35	ПК1
2	Кладовая	2				переток
3	Гостиная-столовая			61	65	ПК2
5	Кухня	60	60			ВР1
6	Ванная	50	75			ВР2
7	Постирочная	1				переток
8	Спальня 2			35	35	ПК3
10	Спальня мастер			68	70	ПК4, ПК5
11	Ванная мастер	50	75			ВР3
	Итого	**163**	**210**	**60**	**205**	

Воздухообмен квартиры — по большей из сумм притока и вытяжки: норма 163 м³/ч, проект 210 м³/ч.
Вытяжка не меньше притока — баланс сведён.

Допущения и предложения на листе

Основа листа: размеры сняты со скана обмерного плана KV design (см): часть подписей не читается, помещения выровнены по читаемым размерам; контрольный обмер не выполнен (К-1); высота потолка 2650 мм принята по отметкам обмера (Н = 2,50…2,66 м, ригель 2,28 м) — уточнить при обмере (К-2); толщины стен 300 / 120 мм приняты, межквартирная стена и колонны — по скану, не замерены (К-1); разрешённая мощность 15 кВт принята по типовым ТУ; при объединении двух квартир — переоформление ТУ (К-4).

Знак «**» — предложение проектировщика, заказчиком не утверждено (согласовать с заказчиком): К-5: дверь пом. 3 (стена Б) — проём в межквартирной стене — объединение квартир, предложение до техзаключения.

См. лист открытых вопросов (лист 6, записи К-1, К-2, К-4, К-5).

Примечания

1. Расчёт систем ОВ и подбор оборудования — проектная организация с допуском СРО; лист даёт места, трассы и привязки.
2. Нормы вытяжки — СП 54.13330.2022 (Изм. 1, 2), табл. 7.1: кухня с электроплитой 60 м³/ч, с газовой 100; ванная и совмещённый санузел 50; уборная 25; гардеробная 0,2 ч⁻¹. Приток в жилые — 3 м³/ч на 1 м² (менее 20 м² общей площади на человека), иначе 30 м³/ч на человека.
3. Вентканалы и шахты не сужать, не переносить и не закрывать; вентилятор и кухонная вытяжка — через обратный клапан, без перекрытия естественной тяги.
4. Проектные расходы — не ниже нормы, вытяжка сведена с притоком вентиляторами мокрых помещений. Клапаны — в простенке у окна, центр 2000 мм, не над кроватью, не ближе 300 мм к стоякам отопления; типоразмер — на расход.
5. Кухонная вытяжка в воздухообмен не включена: воздуховод не менее Ø125 в коробе, вход в канал отдельный.
6. Переток — зазор под полотнами межкомнатных дверей или переточная решётка.
7. Кондиционирование заданием не предусмотрено; при установке трассы фреона и дренажа (не менее 40 мм/м, в К1 через сифон) и питание заложить до черновых работ.
8. Привязки оборудования — по паспортам приобретённых моделей, до черновых работ.

1000 мм · печать 1:1

Изм.	Кол.уч	Лист	№ док.	Подп.	Дата
Разраб.		Кырлан А.С.			18.10.26
Пров.					
ГИП					
Н. контр.					
Утв.					

ГД-2026-009-АИ

Квартира 103 м²

Общая площадь 100,72* м² · * размеры со скана, не замерены (реестр — л. 6, К-1)

Дизайн-проект интерьера

Стадия	Лист	Листов
РП	28	96

План вентиляции

М 1:100

Кырлан Александр Сергеевич

выпуск 18.10.2026 № 53dc234b8d · стр. 34 из 135

План отопления

Радиаторы, стояки, подводки · размеры в мм · высоты от чистого пола

ПРЕДВАРИТЕЛЬНО · не для производства работ · открыто пунктов: 4 (реестр — л. 6)

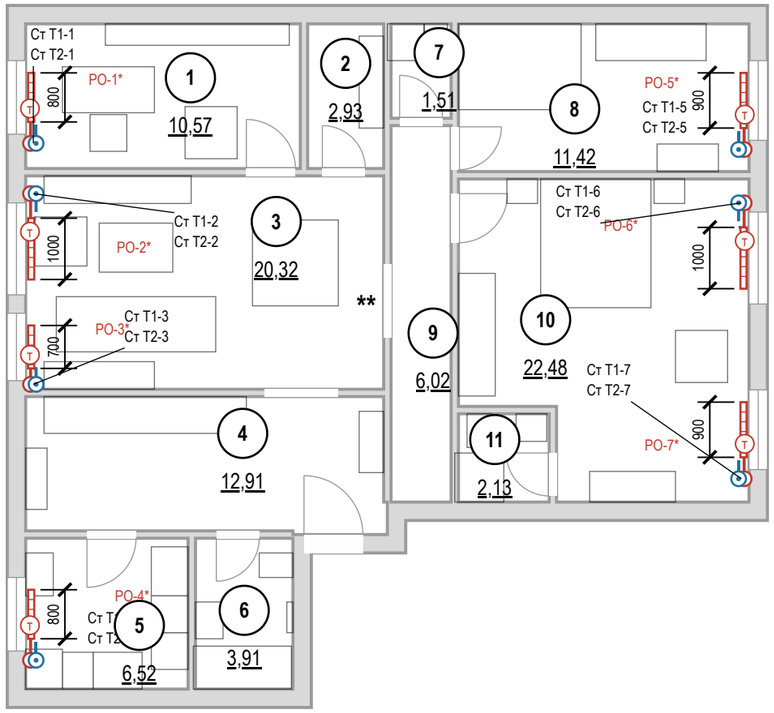

Условные обозначения

- (1) — номер помещения, площадь м²
- радиатор отопления (марка РО-N, длина по плану)
- (Т) — клапан с термоголовкой на подаче
- стояк отопления, подающий (Ст Т1-N)
- стояк отопления, обратный (Ст Т2-N)
- Т1 — отопление, подающий трубопровод
- Т2 — отопление, обратный трубопровод
- ** — «**» — предложение проектировщика, заказчиком не утверждено

Ведомость радиаторов

Марка	Помещение	Тип	Д×В×Г, мм	Низ / стена	Q, Вт
РО-1	1. Кабинет-библиотека	панельный*	800×400×100	120 / 40	расч.
РО-2	3. Гостиная-столовая	панельный*	1000×400×100	120 / 40	расч.
РО-3	3. Гостиная-столовая	панельный*	700×400×100	120 / 40	расч.
РО-4	5. Кухня	панельный*	800×500×100	120 / 40	расч.
РО-5	8. Спальня 2	панельный*	900×500×100	120 / 40	расч.
РО-6	10. Спальня мастер	панельный*	1000×500×100	120 / 40	расч.
РО-7	10. Спальня мастер	панельный*	900×500×100	120 / 40	расч.

* тип и мощность — по теплотехническому расчёту
Низ — от чистого пола, стена — зазор до задней панели, мм.

Привязки — до обмера
Стояки отопления в исходных данных не заданы: показаны у откосов окон, подводки — принципиально. До черновых работ — обмер стояков и паспорта приборов; лист перевыпустить по факту.

Примечания

1. Расчёт системы отопления, теплопотерь и подбор приборов — проектная организация с допуском СРО; лист даёт места и привязки.
2. Тип, длина и мощность радиаторов — по теплотехническому расчёту; лист задаёт места, зазоры и подключение.
3. Радиаторы — под каждым окном жилых комнат и кухни, центр по оси проёма, длина 0,7 ширины окна (кратно 100); окончательно — по расчёту.
4. Зазоры радиатора: низ не менее 100 мм от чистого пола, верх не менее 100 мм до подоконника, 30–50 мм от стены до задней панели; центр по оси окна с допуском ±20 мм.
5. Радиаторы не закрывать глухими коробами и мебелью; перенос и замена приборов в многоквартирном доме — переустройство, согласование с управляющей организацией (ЖК РФ ст. 25–26); вынос на лоджию запрещён.
6. Трубы отопления через межквартирные стены не прокладывать (СП 51.13330.2011, п. 9.19); через перекрытия и перегородки — в гильзах.
7. Привязки приборов и подводок — по паспортам приобретённых радиаторов и клапанов, до черновых работ.
8. До закрытия отделкой трубопроводы отопления испытать гидростатическим давлением с оформлением акта (СП 73.13330.2016, 7.2–7.3).

Допущения и предложения на листе
Основа листа: размеры сняты со скана обмерного плана KV design (см): часть подписей не читается, помещения выровнены по читаемым размерам; контрольный обмер не выполнен (К-1); высота потолка 2650 мм принята по отметкам обмера (Н = 2,50…2,66 м, ригель 2,28 м) — уточнить при обмере (К-2); толщины стен 300 / 120 мм приняты, межквартирная стена и колонны — по скану, не замерены (К-1); разрешённая мощность 15 кВт принята по типовым ТУ; при объединении двух квартир — переоформление ТУ (К-4).
Знак «**» — предложение проектировщика, заказчиком не утверждено (согласовать с заказчиком): К-5: дверь пом. 3 (стена Б) — проём в межквартирной стене — объединение квартир, предложение до техзаключения.
См. лист открытых вопросов (лист 6, записи К-1, К-2, К-4, К-5).

1000 мм · печать 1:1

Изм.	Кол.уч	Лист	№ док.	Подп.	Дата
Разраб.		Кырлан А.С.			18.10.26
Пров.					
ГИП					
Н. контр.					
Утв.					

ГД-2026-009-АИ

Квартира 103 м²

Общая площадь 100,72* м² · * размеры со скана, не замерены (реестр — л. 6, К-1)

Дизайн-проект интерьера

Стадия	Лист	Листов
РП	29	96

План отопления

М 1:100

Кырлан Александр Сергеевич

выпуск 18.10.2026 № 53dc234b8d · стр. 35 из 135

05

Водоснабжение и канализация

Кырлан Александр Сергеевич

выпуск 18.10.2026 · 53dc234b8d · стр. 36 из 135

План выводов сантехники

Выводы В1, Т3, К1 · привязки от чистовых стен · высоты от чистого пола, мм

ПРЕДВАРИТЕЛЬНО · не для производства работ · открыто пунктов: 4 (реестр — л. 6)

Фрагмент 1. Ванная (пом. 6)

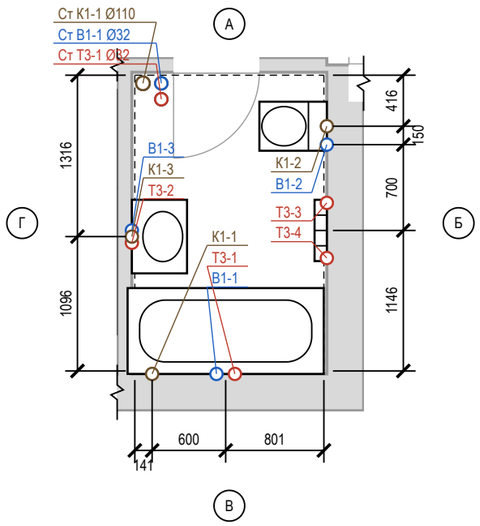

Фрагмент 2. Постирочная (пом. 7)

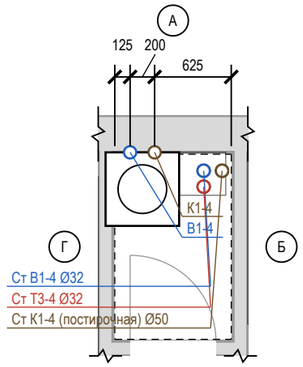

Фрагмент 3. Ванная мастер (пом. 11)

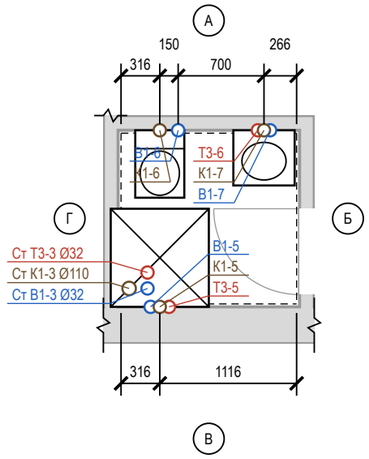

Фрагмент 4. Кухня (пом. 5)

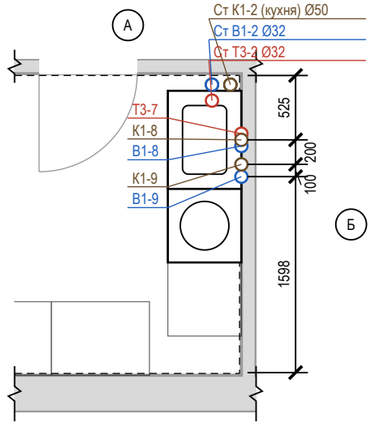

Условные обозначения

- вывод В1 (код — в ведомости привязок)
- вывод Т3 (код — в ведомости привязок)
- вывод К1 (код — в ведомости привязок)
- сантехприбор по расстановке (габарит модели)
- чистовая поверхность стены (от неё привязки)
- стояк «Ст К1-N / Ст В1-N» (ГОСТ 21.601), Ø мм
- линия обрыва (граница фрагмента)
- А — обозначение стены А–Г (как на развёртках)

Ведомость привязок выводов

Код	Прибор	Ø	H, мм	Привязка от чист. стен, мм	Прим.
В1-1	Сн1 ванна	½"	800*	ст. В: 666 от Г	межос. 150
Т3-1	Сн1 ванна	½"	800*	ст. В: 726 от Б	межос. 150
К1-1	Сн1 ванна	Ø50	50*	ст. В: 141 от Г	
В1-2	Сн2 унитаз подвесной	½"	250*	ст. Б: 566 от А	в раме инсталляции
К1-2	Сн2 унитаз подвесной	Ø110	220*	ст. Б: 416 от А	
В1-3	Сн3 умывальник	½"	600*	ст. Г: 1146 от В	межос. 100
Т3-2	Сн3 умывальник	½"	600*	ст. Г: 1046 от В	межос. 100
К1-3	Сн3 умывальник	Ø50	500*	ст. Г: 1096 от В	
Т3-3	Сн4 полотенцесушитель	½"	1150*	ст. Б: 1041 от А	подача, межос. 450; байпас и краны
Т3-4	Сн4 полотенцесушитель	½"	1150*	ст. Б: 921 от В	обратка
В1-4	Пс2 стиральная машина	½"	600*	ст. А: 125 от Г	кран машины
К1-4	Пс2 стиральная машина	Ø50	600*	ст. А: 325 от Г	
В1-5	См1 душ	½"	1200*	ст. В: 241 от Г	межос. 150
Т3-5	См1 душ	½"	1200*	ст. В: 391 от Г	межос. 150
К1-5	См1 душ	Ø50	70*	ст. В: 316 от Г	сифон поддона
В1-6	См2 унитаз подвесной	½"	250*	ст. А: 466 от Г	в раме инсталляции
К1-6	См2 унитаз подвесной	Ø110	220*	ст. А: 316 от Г	
В1-7	См3 умывальник	½"	600*	ст. А: 216 от Б	межос. 100
Т3-6	См3 умывальник	½"	600*	ст. А: 316 от Б	межос. 100
К1-7	См3 умывальник	Ø50	500*	ст. А: 266 от Б	
В1-8	П9 мойка кухонная	½"	600*	ст. Б: 575 от А	межос. 100
Т3-7	П9 мойка кухонная	½"	600*	ст. Б: 475 от А	межос. 100
К1-8	П9 мойка кухонная	Ø50	400*	ст. Б: 525 от А	
В1-9	П10 посудомоечная машина	½"	550*	ст. Б: 825 от А	кран ПММ в шкафу мойки
К1-9	П10 посудомоечная машина	Ø40	550*	ст. Б: 725 от А	слив ПММ в шкафу мойки

* — высота по практике монтажа; сверить по паспорту прибора

Допущения и предложения на листе

Основа листа: размеры сняты со скана обмерного плана KV design (см): часть подписей не читается, помещения выровнены по читаемым размерам; контрольный обмер не выполнен (К-1); высота потолка 2650 мм принята по отметкам обмера (Н = 2,50…2,66 м, ригель 2,28 м) — уточнить при обмере (К-2); толщины стен 300 / 120 мм приняты, межквартирная стена и колонны — по скану, не замерены (К-1); разрешённая мощность 15 кВт принята по типовым ТУ; при объединении двух квартир — переоформление ТУ (К-4).

См. лист открытых вопросов (лист 6, записи К-1, К-2, К-4).

Примечания

1. Привязки выводов даны от чистовых поверхностей стен (облицовка на сторону: ванная — 24 мм (штукатурка 10 + клей 5 + плитка 9); постирочная — 15 мм (штукатурка 10 + шпаклёвка 5 (принято)); ванная мастер — 24 мм (штукатурка 10 + клей 5 + плитка 9); кухня — 22 мм (фартук: штукатурка 10 + клей 3 + плитка 9)); эти же грани — на развёртках и в раскладке плитки. Высоты — от чистого пола помещения.
2. Высоты и межосевые, отмеченные «*», приняты по практике монтажа; до черновой разводки сверить по паспорту выбранного прибора (смеситель, инсталляция, сифон).
3. Горячая вода (Т3) — слева от холодной (В1), если смотреть на прибор. Допуск установки выводов: ±5 мм в группе, ±20 мм у отдельно стоящих.
4. Расчёт систем водоснабжения и канализации и подбор оборудования выполняет проектная организация; лист задаёт места и высоты выводов.
5. Посудомоечная машина П10: кран и слив — отдельными выводами в шкафу мойки (не за машиной), до машины ≤ 1500 мм.
6. Прибор П9 мойка кухонная, П10 посудомоечная машина взят из расстановки мебели (по шкафу с мойкой).

1000 мм · печать 1:1

Изм.	Кол.уч	Лист	№ док.	Подп.	Дата
Разраб.		Кырлан А.С.			18.10.26
Пров.					
ГИП					
Н. контр.					
Утв.					

ГД-2026-009-АИ

Квартира 103 м²

Общая площадь 100,72* м² · * размеры со скана, не замерены (реестр — л. 6, К-1)

Дизайн-проект интерьера

Стадия	Лист	Листов
РП	30	96

План выводов сантехники

М 1:50

Кырлан Александр Сергеевич

выпуск 18.10.2026 № 53dc234b8d · стр. 37 из 135

Схема разводки водопровода и канализации

Схемы систем В1, Т3, К1 · трассы принципиальные · уклоны в мм на 1 м · план М 1:200, фрагменты М 1:40

ПРЕДВАРИТЕЛЬНО · не для производства работ · открыто пунктов: 4 (реестр — л. 6)

План квартиры (М 1:200)

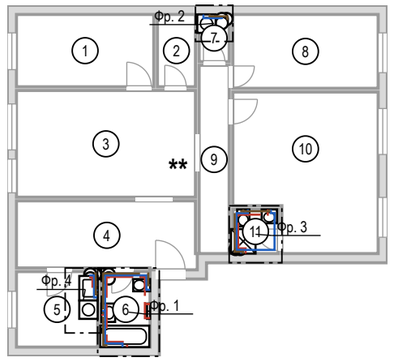

Узел ввода В1, Т3 (схема, без масштаба)

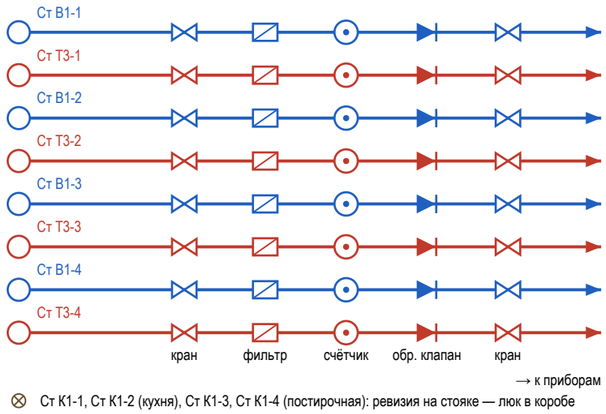

⊗ Ст К1-1, Ст К1-2 (кухня), Ст К1-3, Ст К1-4 (постирочная): ревизия на стояке — люк в коробе

Условные обозначения

- В1 — водопровод хозяйственно-питьевой (ХВС), PP-R Ø20
- Т3 — горячее водоснабжение, подача (ГВС), PP-R Ø20
- К1 — канализация бытовая
- направление уклона К1 / пола: Ø, мм на 1 м
- ⊗ ревизия (прочистка) К1 — доступ сохранить
- • тройник (ответвление к прибору)
- короб К1 над чистым полом (ГКЛВ под плитку)
- ○ вывод В1 (код — в ведомости привязок)
- ○ вывод Т3 (код — в ведомости привязок)
- ○ вывод К1 (код — в ведомости привязок)
- сантехприбор по расстановке (габарит модели)
- ◯ стояк «Ст К1-N / Ст В1-N» (ГОСТ 21.601), Ø мм
- линия обрыва (граница фрагмента)
- граница фрагмента на плане (Фр. N)

Фр. 1. Ванная (М 1:40)

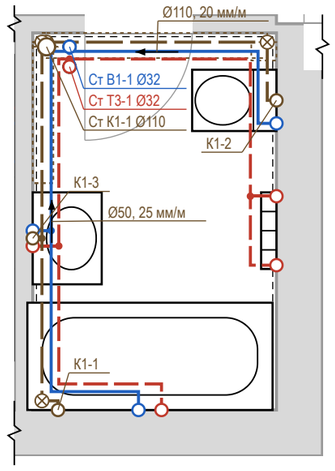

Фр. 2. Постирочная (М 1:40)

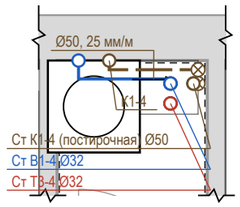

Фр. 3. Ванная мастер (М 1:40)

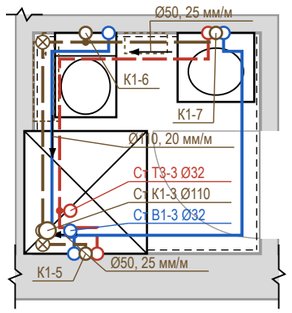

Фр. 4. Кухня (М 1:40)

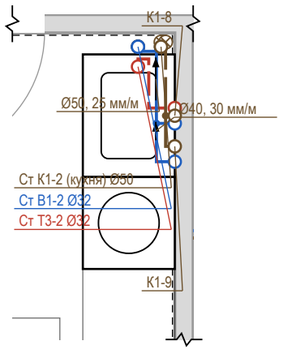

Профиль выпусков К1 (до врезки в стояк)

Выпуск	Прибор	Ø	L, м	i, мм/м	Δh, мм	Прокладка, мм
К1-2	Сн2 унитаз подвесной	Ø110	1,91	20	38	под дверью — перенести выпуск
К1-6	См2 унитаз подвесной	Ø110	1,60	20	32	короб 180×140
К1-1	Сн1 ванна	Ø50	2,56	25	64	короб 150×110
К1-7	См3 умывальник	Ø50	2,45	25	61	короб 150×110
К1-3	Сн3 умывальник	Ø50	1,40	25	35	короб 120×110
К1-4	Пс2 стиральная машина	Ø50	0,76	25	19	над полом за приборами
К1-8	П9 мойка кухонная	Ø50	0,60	25	15	в полу, стяжка ≥ 110
К1-5	См1 душ	Ø50	0,46	25	12	над полом за приборами
К1-9	П10 посудомоечная машина	Ø40	0,80	30	24	в полу, стяжка ≥ 109

Короб h×b: h — от чистого пола, b — от чистовой стены. Стяжка 35 мм — лист полов.

Допущения и предложения на листе

Основа листа: размеры сняты со скана обмерного плана KV design (см): часть подписей не читается, помещения выровнены по читаемым размерам; контрольный обмер не выполнен (К-1); высота потолка 2650 мм принята по отметкам обмера (Н = 2,50…2,66 м, ригель 2,28 м) — уточнить при обмере (К-2); толщины стен 300 / 120 мм приняты, межквартирная стена и колонны — по скану, не замерены (К-1); разрешённая мощность 15 кВт принята по типовым ТУ; при объединении двух квартир — переоформление ТУ (К-4).

Знак «**» — предложение проектировщика, заказчиком не утверждено (согласовать с заказчиком): К-5: дверь пом. 3 (стена Б) — проём в межквартирной стене — объединение квартир, предложение до техзаключения.

См. лист открытых вопросов (лист 6, записи К-1, К-2, К-4, К-5).

Примечания

1. Трассы принципиальные, построены от стояков вдоль стен помещений; фактическое положение фиксируется исполнительной схемой с привязками (фото с рулеткой) до закрытия.
2. Уклон К1 не менее 1/d и не более 150 мм/м (СП 30.13330.2020, п. 19.1), приняты практические уклоны; поворот — двумя отводами 45°, ревизия после поворота, доступ сохранить. Стояк К1 в коробе — звукоизоляция стояка в коробе, без жёсткого контакта короба с трубой.
3. Решение по К1: стяжка 35 мм не укрывает трубы (нужно Ø + Δh + 45 мм) — выпуски идут над чистым полом вдоль стен: К1-4, К1-5 — за приборами и в раме инсталляции; К1-2, К1-6, К1-1, К1-7, К1-3 — в коробе ГКЛВ под плитку (размеры в профиле). Короба — на развёртках; отметку низа врезки в стояк замерить до черновых работ.
4. Трасса К1 от К1-2 проходит под дверным проёмом — короб там невозможен: выпуск перенести или вести в полу с подъёмом пола помещения.
5. На каждом вводе В1 и Т3 — кран шаровой, фильтр, счётчик, обратный клапан; доступ через люк не меньше 300×400. Водопровод — в штробе стен или в коробах; трубы испытать давлением до закрытия (акт скрытых работ).
6. Расчёт систем, диаметры магистралей и подбор оборудования выполняет проектная организация; врезка и перенос стояков — по согласованию с управляющей организацией. Арматуру и привязки сверить по паспортам приборов.

Изм.	Кол.уч	Лист	№ док.	Подп.	Дата
Разраб.		Кырлан А.С.			18.10.26
Пров.					
ГИП					
Н. контр.					
Утв.					

ГД-2026-009-АИ

Квартира 103 м²

Общая площадь 100,72* м² · * размеры со скана, не замерены (реестр — л. 6, К-1)

Дизайн-проект интерьера

Стадия	Лист	Листов
РП	31	96

Схема разводки водопровода и канализации

М б/м

Кырлан Александр Сергеевич

выпуск 18.10.2026 № 53dc234b8d · стр. 38 из 135

Спецификация сантехнического оборудования

Форма 1 ГОСТ 21.110-2013 · ГД-2026-009-АИ-ВК.СО · приборы, арматура, трубопроводы

ПРЕДВАРИТЕЛЬНО · не для производства работ · открыто пунктов: 4 (реестр — л. 6)

Поз.	Наименование и техническая характеристика	Тип, марка, обозначение документа	Код продукции	Поставщик	Ед. изм.	Кол.	Масса 1 ед., кг	Примечание
	Санитарные приборы							
1	Ванна акриловая 1600×700 мм, с каркасом, экраном и отверстием слив-перелив	аналог		выбор заказчика	шт	1		Сн1
2	Унитаз подвесной безободковый, с сиденьем микролифт, крепёж и звукоизолирующая прокладка	Jacob Delafon Struktura EDF102-00		выбор заказчика	шт	2		Сн2, См2
3	Инсталляция для подвесного унитаза: рама высотой 1120 мм, бачок, клавиша смыва (ось клавиши 1050 мм от чистого пола)	аналог		выбор заказчика	шт	2		Сн2, См2; короб ГКЛВ
4	Умывальник подвесной 600×450 мм, с отверстием под смеситель и переливом	аналог		выбор заказчика	шт	1		Сн3
5	Умывальник подвесной 500×450 мм, с отверстием под смеситель и переливом	аналог		выбор заказчика	шт	1		См3
6	Поддон душевой низкий 800×800 мм, с сифоном и выпуском Ø50, на ножках/подиуме	аналог		выбор заказчика	шт	1		См1
7	Мойка кухонная 600×800 мм, с переливом	аналог		с кухонной мебелью	шт	1		П9
8	Полотенцесушитель водяной (ГВС), с байпасом и кранами	аналог		выбор заказчика	шт	1		Сн4
	Смесители, сифоны и арматура приборов							
9	Смеситель для ванны настенный однорычажный, межосевое 150 мм, с душевым набором (лейка, шланг, держатель)	аналог		выбор заказчика	шт	1		Сн1
10	Смеситель для умывальника однорычажный, с донным клапаном	аналог		выбор заказчика	шт	2		Сн3, См3
11	Душевая система скрытого монтажа с термостатом: встраиваемая часть, верхний душ, ручная лейка	аналог		выбор заказчика	шт	1		См1; встраиваемая часть — до плитки
12	Смеситель кухонный однорычажный, высокий излив	аналог		выбор заказчика	шт	1		П9
13	Обвязка ванны слив-перелив Ø40/50 с сифоном	аналог		выбор заказчика	шт	1		Сн1
14	Сифон для умывальника бутылочный Ø32/40–50, с гофрой к выпуску	аналог		выбор заказчика	шт	2		Сн3, См3
15	Сифон для мойки с отводом для ПММ Ø40/50	аналог		выбор заказчика	шт	1		П9
16	Сифон для стиральной машины встраиваемый в стену Ø50, с обратным клапаном	аналог		выбор заказчика	шт	1		Пс2
17	Кран угловой ½"×½" с гибкой подводкой 40 см (умывальники, мойка)	аналог		выбор заказчика	шт	6		по 2 на прибор
18	Кран шаровой угловой ½"×¾" для подключения стиральной и посудомоечной машины	аналог		выбор заказчика	шт	2		Пс2, П10
19	Узел подключения полотенцесушителя: байпас Ду20, краны шаровые ½" ×2	аналог		выбор заказчика	шт	1		
	Трубопроводы							
20	Труба полипропиленовая PP-R PN20 Ø20×3,4 (В1)	ГОСТ 32415-2013		выбор заказчика	м	19	0,17	11,4 + 5,5 + 10 %
21	Труба PP-R, армированная стекловолокном, PN20 Ø20×2,8 (Т3)	ГОСТ 32415-2013		выбор заказчика	м	17,5	0,15	9,4 + 6,1 + 10 %
22	Труба канализационная ПП Ø40 (К1)	ГОСТ 32414-2013		выбор заказчика	м	1		0,3 + 0,6 + 10 %
23	Труба канализационная ПП Ø50 (К1)	ГОСТ 32414-2013		выбор заказчика	м	8,5		5,3 + 2,1 + 10 %
24	Труба канализационная ПП Ø110 (К1)	ГОСТ 32414-2013		выбор заказчика	м	4,5		3,5 + 0,4 + 10 %
	Фасонные части и выводы							
25	Отвод канализационный ПП 45° Ø40	ГОСТ 32414-2013		выбор заказчика	шт	2		2 шт. на поворот
26	Отвод канализационный ПП 45° Ø50	ГОСТ 32414-2013		выбор заказчика	шт	24		2 шт. на поворот
27	Отвод канализационный ПП 45° Ø110	ГОСТ 32414-2013		выбор заказчика	шт	12		2 шт. на поворот
28	Тройник канализационный ПП 45° (врезки ветвей)	ГОСТ 32414-2013		выбор заказчика	шт	8		
29	Ревизия канализационная ПП (после поворота трассы)	ГОСТ 32414-2013		выбор заказчика	шт	11		доступ сохранить
30	Фитинги PP-R Ø20: тройники, угольники 90° (ветви и повороты В1, Т3)	ГОСТ 32415-2013		выбор заказчика	шт	46		
31	Водорозетка PP-R Ø20×½" настенная, с креплением	ГОСТ 32415-2013		выбор заказчика	шт	16		коды — лист выводов
	Узлы ввода, люки, короба							
32	Кран шаровой латунный Ду15 PN16 (отключение ввода)	аналог		выбор заказчика	шт	8		Ст В1-1, Ст Т3-1, Ст В1-2, Ст Т3-2, Ст В1-3, Ст Т3-3, Ст В1-4, Ст Т3-4
33	Фильтр сетчатый косой Ду15	аналог		выбор заказчика	шт	8		
34	Счётчик воды крыльчатый Ду15 (ХВ, ГВ), с поверкой	аналог		выбор заказчика	шт	8		пломба УК
35	Клапан обратный Ду15	аналог		выбор заказчика	шт	8		
36	Люк ревизионный нажимной под плитку 300×400 мм	аналог		выбор заказчика	шт	4		к стоякам и арматуре
37	Звукоизоляция стояка К1 в коробе: рулонный звукоизоляционный материал ≥ 10 мм, обмотка стояка на высоту этажа	аналог		выбор заказчика	м	10,8		Ст К1-1, Ст К1-2 (кухня), Ст К1-3, Ст К1-4 (постирочная)
38	Короб К1 над полом: профиль ПН/ПС, ГКЛВ 12,5 мм под плитку	аналог		выбор заказчика	м	5,4		сечение — лист разводки

Примечания

1. Форма 1 ГОСТ 21.110-2013, ширины граф изменены по п. 4.1. «Аналог» — аналог по характеристикам: модели внести до черновых работ, привязки выводов сверить по паспортам.
2. Бытовая техника не входит (показана арматура подключения), мойка — в комплекте кухни. Длины труб — трасса листа разводки + подъёмы + 10 %.
3. Стояк К1 в коробе — звукоизоляция стояка в коробе без жёсткого контакта короба с трубой.
4. Расчёт систем водоснабжения и канализации, диаметры магистралей и подбор оборудования выполняет проектная организация.

Допущения и предложения на листе

Основа листа: размеры сняты со скана обмерного плана KV design (см): часть подписей не читается, помещения выровнены по читаемым размерам; контрольный обмер не выполнен (К-1); высота потолка 2650 мм принята по отметкам обмера (Н = 2,50…2,66 м, ригель 2,28 м) — уточнить при обмере (К-2); толщины стен 300 / 120 мм приняты, межквартирная стена и колонны — по скану, не замерены (К-1); разрешённая мощность 15 кВт принята по типовым ТУ; при объединении двух квартир — переоформление ТУ (К-4).
См. лист открытых вопросов (лист 6, записи К-1, К-2, К-4).

Изм.	Кол.уч	Лист	№ док.	Подп.	Дата

ГД-2026-009-АИ

Квартира 103 м²

Общая площадь 100,72* м² · * размеры со скана, не замерены (реестр — л. 6, К-1)

Разраб.	Кырлан А.С.		18.10.26
Пров.			
ГИП			
Н. контр.			
Утв.			

Дизайн-проект интерьера

Стадия	Лист	Листов
РП	32	96

Спецификация сантехнического оборудования

М б/м

Кырлан Александр Сергеевич

выпуск 18.10.2026 № 53dc234b8d · стр. 39 из 135

Спецификация светильников и сценарии освещения

Светильники, ленты и блоки питания, слои света и сценарии по помещениям · б/м

Спецификация светильников

Поз.	Марки	Наименование	Установка	Кол.	P, Вт	Σ P, Вт	Ф, лм	Тц, К	Ra	Угол, °	IP	Дим.	Группа	Пом.
1	Св17–Св22	Встраиваемый точечный	встраиваемый	12	12	144	1050	2700	90	—	20	—	L7	1, 8
2	Св23	Лента светодиодная 24 В	в коробе, профиль с рассеивателем	24,6 м	9,6/м	236,2	900/м	2700	90	—	20	да	L8	1, 8
3	Св10, Св11, Св24, Св25	Настенный (бра)	на стене, H=1500	6	6	36	400	2700	90	60	20	да	L3, L9	1, 8, 10
4	Св16	Потолочный накладной	на потолке, засветка стены	2	10	20	900	3000	90	—	20	—	L6	2, 7
5	Св1–Св8, Св31–Св37	Встраиваемый точечный	встраиваемый	15	12	180	1000	3000	90	—	20	—	L1, L4	3, 5
6	Св9	Подвесной	подвес, низ H=1600	1	15	15	1200	2700	90	—	20	—	L2	3
7	Св10	Лента светодиодная 24 В	в коробе, профиль с рассеивателем	5 м	9,6/м	48	900/м	2700	90	—	20	да	L3	3
8	Св26–Св29, Св53, Св54	Встраиваемый точечный	встраиваемый	6	7	42	600	3000	90	—	20	—	L10	4, 9
9	Св30	Лента светодиодная 24 В	в коробе, профиль с рассеивателем, датчик движения	1,8 м	4,8/м	8,6	150/м	2700	90	—	20	нет	L11	4
10	Св38, Св39	Линейный светильник	на поверхности	1,2 м	8	16	700	3000	90	—	20	—	L5	5
11	Св12–Св14, Св51	Встраиваемый точечный	встраиваемый	4	6	24	500	3000	90	—	44	—	L4, L17	6, 11
12	Св15, Св52	Настенный светильник над зеркалом, драйвер встроен	над зеркалом, H=1900	2	8	16	600	3000	90	—	44	—	L5, L18	6, 11
13	Св1–Св8	Встраиваемый точечный	встраиваемый	8	12	96	1000	2700	90	—	20	—	L1	10
14	Св9	Лента светодиодная 24 В	в коробе, профиль с рассеивателем	15,5 м	9,6/м	148,8	900/м	2700	90	—	20	да	L2	10
15	Св50	Встраиваемый точечный	встраиваемый	1	7	7	600	3000	90	—	44	—	L17	11
		Итого		**57 шт + 48,1 м**		**1037,6**								

Слои света по помещениям

Пом.	Помещение	Слои света и группы включения (марки светильников)	Тц, К	Ra	Σ P, Вт	Сцен.
1	Кабинет-библиотека	общий — L7 (Св17–Св22); рабочий — L9 (Св24, Св25); акцентный — L8 (Св23)	2700	90	202,1	1
2	Кладовая	общий — L6 (Св16)	3000	90	10	—
3	Гостиная-столовая	общий — L1 (Св1–Св8); рабочий — L2 (Св9); акцентный — L3 (Св10)	2700 / 3000	90	159	4
4	Прихожая-холл	общий — L10 (Св26–Св29); ночной — L11 (Св30)	2700 / 3000	90	36,6	—
5	Кухня	общий — L4 (Св31–Св37); рабочий — L5 (Св38, Св39)	3000	90	100	—
6	Ванная	общий — L4 (Св12–Св14); рабочий — L5 (Св15)	3000	90	26	—
7	Постирочная	общий — L6 (Св16)	3000	90	10	—
8	Спальня 2	общий — L7 (Св17–Св22); рабочий — L9 (Св24, Св25); акцентный — L8 (Св23)	2700	90	202,1	1
9	Коридор	общий — L10 (Св53, Св54)	3000	90	14	—
10	Спальня мастер	общий — L1 (Св1–Св8); рабочий — L3 (Св10, Св11); акцентный — L2 (Св9)	2700	90	256,8	2
11	Ванная мастер	общий — L17 (Св50, Св51); рабочий — L18 (Св52)	3000	90	21	—

Примечания

1. Позиции и марки Св — те же, что на плане освещения (лист 21) и в ведомости светильников (лист 23); группы L — по плану выключателей (лист 22).
2. Модели светильников не назначены: подбор по графам спецификации — поток, Тц, Ra, угол, IP и диммирование не хуже указанных, мощность не больше. IP 20 — сухие помещения.
3. Длина LED-ленты в карнизе — по линии карниза плана потолков (лист 34); Σ P = Вт/м × длина. Блок питания загружен не больше чем на 80 %; лента 24 В длиннее 10 м питается с двух концов; доступ к блоку питания — люк ревизии 300×300 мм или место, указанное в таблице.
4. Сценарии: уровень — доля максимальной яркости группы, %; 0 — группа выключена. Уровень ниже 100 % — только у групп на светорегуляторе (задний фронт, ТЕ) с диммируемыми драйверами и блоками питания.
5. Мощность и поток — по паспортам принятых изделий, Σ P — установленная мощность освещения. Оценка освещённости — на плане освещения; это не светотехнический расчёт.

Допущения и предложения на листе. Основа листа: размеры сняты со скана обмерного плана KV design (см): часть подписей не читается, помещения выровнены по читаемым размерам; контрольный обмер не выполнен (К-1); высота потолка 2650 мм принята по отметкам обмера (H = 2,50…2,66 м, ригель 2,28 м) — уточнить при обмере (К-2); толщины стен 300 / 120 мм приняты, межквартирная стена и колонны — по скану, не замерены (К-1); разрешённая мощность 15 кВт принята по типовым ТУ; при объединении двух квартир — переоформление ТУ (К-4). Знак «**» — предложение проектировщика, заказчиком не утверждено (согласовать с заказчиком): записи в реестре нет: S2 — светорегулятор добавлен под диммируемую ленту L3; уровни сценариев выбраны конвейером. См. лист открытых вопросов (лист 6, записи К-1, К-2, К-4).

LED-ленты, линейные светильники и блоки питания

Марка	Пом.	L, м	U, В	Вт/м	Σ P, Вт	БП	P БП, Вт	Загр., %	Питание	Доступ к БП
Св23	1	12,3	24	9,6	118,1	БП2	200	126	с двух концов	люк 300×300 в коробе У1 у окна
Св10	3	5	24	9,6	48	БП1	200	98	с одного конца	люк 300×300 в коробе У1 у входа
Св30	4	1,8	24	4,8	8,6	БП3	20	43	с одного конца	в шкафу М16, верхняя полка
Св38	5	0,6	24	—	8	БП2	200	126	встроенный ввод	люк 300×300 в коробе У1 у окна
Св39	5	0,6	24	—	8	БП2	200	126	встроенный ввод	люк 300×300 в коробе У1 у окна
Св23	8	12,3	24	9,6	118,1	БП2	200	126	с двух концов	люк 300×300 в коробе У1 у окна
Св9	10	15,5	24	9,6	148,8	БП1	200	98	с двух концов	люк 300×300 в коробе У1 у входа

Сценарии освещения

Пом.	Сценарий	Группы и уровни, %	Чем включается
1	Вечер	L7 споты — 0; L8 подсветка короба — 100; L9 бра — 100	S4, S5, S6
3	Вечер	L1 общий свет (споты) — 0; L2 подвес над обеденным столом — 100; L3 лента в карнизе (диммер) — 50	S1, S2**, S2** светорегулятор, S3
3	Гости	L1 общий свет (споты) — 100; L2 подвес над обеденным столом — 100; L3 лента в карнизе (диммер) — 100	S1, S2**, S2** светорегулятор, S3
3	Кино	L1 общий свет (споты) — 0; L2 подвес над обеденным столом — 0; L3 лента в карнизе (диммер) — 20	S2**, S2** светорегулятор, S3
3	Уборка	L1 общий свет (споты) — 100; L2 подвес над обеденным столом — 100; L3 лента в карнизе (диммер) — 0	S1, S2**, S3
8	Вечер	L7 споты — 0; L8 подсветка короба — 100; L9 бра — 100	S4, S5, S6
10	Вечер	L1 общий свет (споты) — 0; L2 подвес над обеденным столом — 100; L3 лента в карнизе (диммер) — 100	S1, S2**, S2** светорегулятор, S3
10	Уборка	L1 общий свет (споты) — 100; L2 подвес над обеденным столом — 100; L3 лента в карнизе (диммер) — 0	S1, S2**, S3

Слои света

общий — равномерный свет помещения, по норме освещённости

рабочий — местный свет задачи: столешница, зеркало, чтение у кровати

акцентный — подсветка потолка, стен и ниш; не входит в поток общего света

ночной — путь спальня → санузел: не выше 2700 К, малая яркость, датчик движения

Изм.	Кол.уч	Лист	№ док.	Подп.	Дата
Разраб.		Кырлан А.С.			18.10.26
Пров.					
ГИП					
Н. контр.					
Утв.					

ГД-2026-009-АИ

Квартира 103 м²

Общая площадь 100,72* м² · * размеры со скана, не замерены (реестр — л. 6, К-1)

Дизайн-проект интерьера

Стадия	Лист	Листов
РП	33	96

Спецификация светильников и сценарии освещения
М б/м

Кырлан Александр Сергеевич

выпуск 18.10.2026 № 53dc234b8d · стр. 40 из 135

06

Потолки и ГКЛ-конструкции

Кырлан Александр Сергеевич

выпуск 18.10.2026 · 53dc234b8d · стр. 41 из 135

План потолков

Уровни и марки потолков, короба с подсветкой, ниши под шторы, люки, вырезы · отметки низа от ±0,000 чистого пола · размеры в мм

ПРЕДВАРИТЕЛЬНО · не для производства работ · открыто пунктов: 4 (реестр — л. 6)

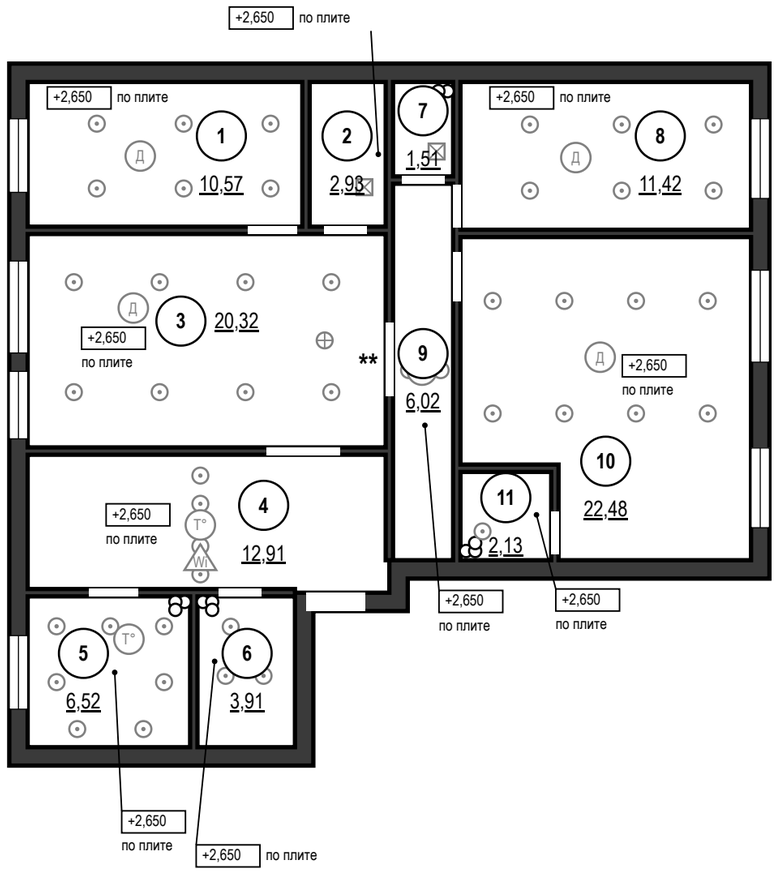

Ведомость потолков

Пом.	Марка	Конструкция	Низ	S, м²	Q
1		по плите, окраска	+2,650	10,57	
2		по плите, окраска	+2,650	2,93	
3		по плите, окраска	+2,650	20,32	
4		по плите, окраска	+2,650	12,91	
5		по плите, окраска	+2,650	6,52	
6		по плите, окраска	+2,650	3,91	
7		по плите, окраска	+2,650	1,51	
8		по плите, окраска	+2,650	11,42	
9		по плите, окраска	+2,650	6,02	
10		по плите, окраска	+2,650	22,48	
11		по плите, окраска	+2,650	2,13	
		Итого		**100,72**	

Ведомость вырезов и закладных в потолке

Марка	Устройство	Кол.	Пом.
	Светильник встраиваемый (марки — план освещения)	46	1, 3, 4, 5, 6, 8, 9, 10, 11
	Светильник накладной (марки — план освещения)	2	2, 7
	Светильник подвесной (марки — план освещения)	1	3
ИП2, ИП1, ИП2, ИП1	Извещатель дымовой	4	1, 3, 8, 10
ИП3, ИП4, ИП6	Извещатель тепловой	3	4, 5, 9
AP1**	Точка доступа Wi-Fi, PoE	1	4

Условные обозначения

- потолок по плите перекрытия, окраска, низ +2,650
- светильник встраиваемый — подложка с плана освещения
- светильник накладной — подложка с плана освещения
- светильник подвесной — подложка с плана освещения
- Д — извещатель дымовой на потолке — подложка
- T° — извещатель тепловой на потолке — подложка
- Wi — точка доступа Wi-Fi на потолке — подложка
- +2,6 — отметка низа потолка, м; под ней марка потолка
- 1 — номер помещения, площадь м²

Допущения и предложения на листе

Основа листа: размеры сняты со скана обмерного плана KV design (см): часть подписей не читается, помещения выровнены по читаемым размерам; контрольный обмер не выполнен (К-1); высота потолка 2650 мм принята по отметкам обмера (Н = 2,50…2,66 м, ригель 2,28 м) — уточнить при обмере (К-2); толщины стен 300 / 120 мм приняты, межквартирная стена и колонны — по скану, не замерены (К-1); разрешённая мощность 15 кВт принята по типовым ТУ; при объединении двух квартир — переоформление ТУ (К-4).

Знак «**» — предложение проектировщика, заказчиком не утверждено (согласовать с заказчиком): К-5: дверь пом. 3 (стена Б) — проём в межквартирной стене — объединение квартир, предложение до техзаключения; записи в реестре нет: AP1 — точка доступа Wi-Fi: число и места.

Открытые вопросы и конфликты по листу: К-2.

См. лист открытых вопросов (лист 6, записи К-1, К-2, К-4, К-5).

Примечания

1. За отметку ±0,000 принят уровень чистого пола сухих помещений (готовое покрытие), а не существующего пола; пол пом. 6, 11 — −0,015; существующий пол снимается до плиты, его отметка не замерена. Отметки в прямоугольниках — низ потолка; низ плиты перекрытия +2,650. Марка потолка — одна конструкция и отметка на весь альбом.
2. Светильники и потолочные устройства — подложка с планов освещения, слаботочных систем и вентиляции (положение — по ним); вырезы и закладные — по ведомости на листе, до обшивки; отверстия не совмещать с профилями.
3. Пом. 1, 2, 3, 4, 5, 6, 7, 8, 9, 10, 11 — потолок по плите без подвесной системы; отделка — по ведомости отделки.

1000 мм · печать 1:1

Изм.	Кол.уч	Лист	№ док.	Подп.	Дата
Разраб.		Кырлан А.С.			18.10.26
Пров.					
ГИП					
Н. контр.					
Утв.					

ГД-2026-009-АИ

Квартира 103 м²

Общая площадь 100,72* м² · * размеры со скана, не замерены (реестр — л. 6, К-1)

Дизайн-проект интерьера

Стадия	Лист	Листов
РП	34	96

План потолков

М 1:100

Кырлан Александр Сергеевич

выпуск 18.10.2026 № 53dc234b8d · стр. 42 из 135

Раскладка плитки. Планы полов

Раскладка от чистовых размеров · размеры в мм · отметки от ±0,000

Фрагмент 1. Ванная (пом. 6). Пол 600×600, шов 2 мм, М 1:20

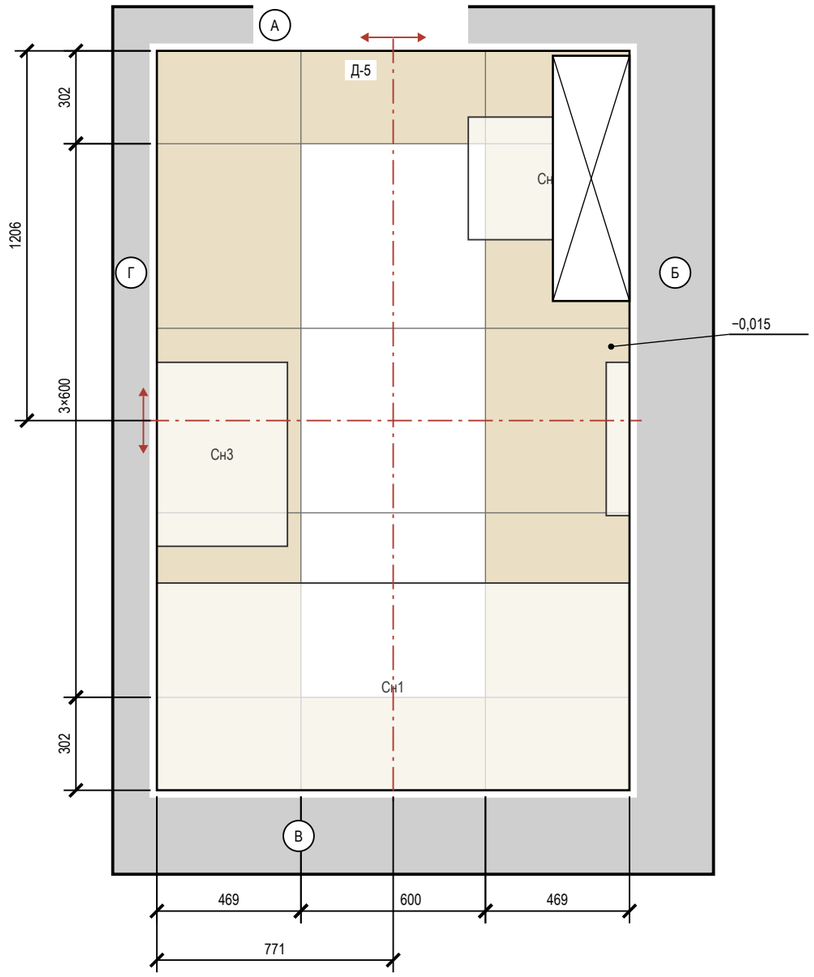

Фрагмент 2. Ванная мастер (пом. 11). Пол 600×600, шов 2 мм, М 1:20

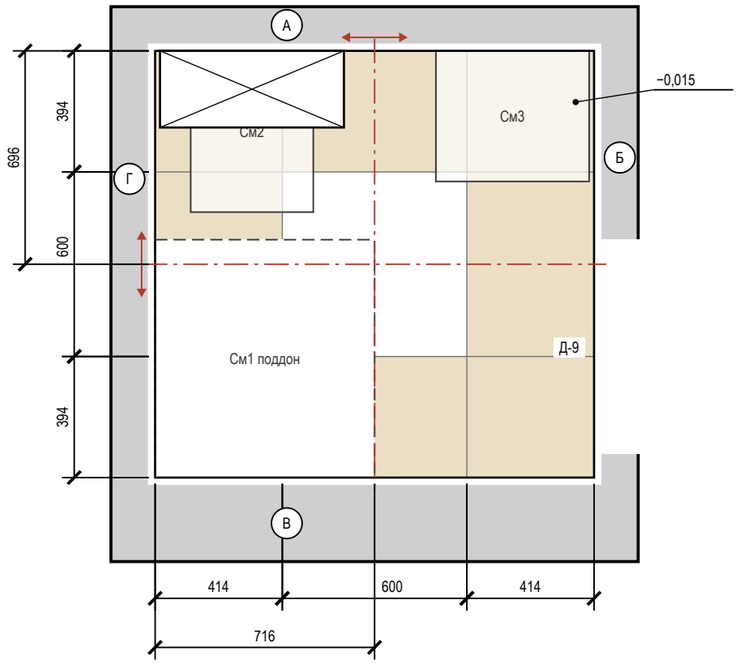

Примечания

1. Раскладка от чистовых размеров: стены санузлов теряют 10 + 5 + 9 = 24 мм на сторону (штукатурка, клей, плитка); подрезки — чистые, без шва.
2. Старт — от центра помещения (штрихпунктир, стрелки — направление укладки); размер старта — от чистовых стен Г и А.
3. Раскладка пола «Прихожая-холл» — на листе «Раскладка плитки. Прихожая-холл».
4. Калибр партии не задан — до укладки замерить (рабочий размер W, ГОСТ 13996-2019) и пересчитать подрезки.
5. Количество: целые по раскладке + по одной на подрезку, запас 10 %; один артикул — одна партия и тон. Исключены поддон, короб, проёмы и места за коробом; S — по чистым граням: стены нетто = зона облицовки по ведомости отделки − место за коробом инсталляции 1,68 м² (плитку за коробом не кладут), короб — отдельной строкой.
6. Клей C2 TE S1 Ceresit CM 17; C2 TE S1 (ГОСТ Р 56387-2018), затирка CG2WA Mapei Ultracolor Plus 132; CG2WA; расход — по ТУ выбранной марки.
7. Гидроизоляция: пол и стены 200 мм от ЧП; над ванной — до 2000 и 300 мм за борт, у душа до 2000 и 500 мм за поддон (см. развёртки); акт скрытых работ, пролив 24 ч.
8. Швы пола совмещены со швами стены А; по периметру — демпферная лента.
9. Отметка чистого пола −0,015, порог 15 мм; стык с соседним покрытием — по оси полотна двери.

Ведомость плитки

Помещение, поверхность	Плитка, код	Формат	Шов	S, м²	Целых	Подр.	С запасом
Ванная, пол	аналог: керамогранит под травертин	600×600	2	3,91	3	12	17
Ванная, стены А–Г	аналог: керамогранит под травертин	600×1200	2	17,04	13	19	36
Ванная, короб инсталляции	аналог: керамогранит под травертин	600×1200	2	1,76	0	6	7
Ванная мастер, пол	аналог: керамогранит под травертин	600×600	2	2,13	0	8	9
Ванная мастер, стены А–Г	аналог: керамогранит под травертин	600×1200	2	11,85	5	19	28
Ванная мастер, короб инсталляции	аналог: керамогранит под травертин	600×1200	2	1,47	1	3	5
Прихожая-холл, пол	A8UZ	600×1200	2	12,91	0	20	22
Итого 600×600				6,04	3	20	26
Итого 600×1200				**45,03**	**19**	**67**	**98**

Условные обозначения

- плитка целая; тонкая линия — шов
- плитка с подрезкой (размер — на цепочке)
- ось старта; стрелки — направление укладки
- сантехприбор: габарит, высота по практике
- поддон душа — плитку пола под ним не кладут
- короб инсталляции: плитка пола — до короба
- отметка чистого пола на полке выноски, м
- А — обозначение стены А–Г (как на развёртках)

Допущения и предложения на листе

Основа листа: размеры сняты со скана обмерного плана KV design (см): часть подписей не читается, помещения выровнены по читаемым размерам; контрольный обмер не выполнен (К-1); высота потолка 2650 мм принята по отметкам обмера (Н = 2,50…2,66 м, ригель 2,28 м) — уточнить при обмере (К-2); толщины стен 300 / 120 мм приняты, межквартирная стена и колонны — по скану, не замерены (К-1); разрешённая мощность 15 кВт принята по типовым ТУ; при объединении двух квартир — переоформление ТУ (К-4).
См. лист открытых вопросов (лист 6, записи К-1, К-2, К-4).

Ведомость материалов

Материал	Класс, код	Норма расхода	Кол-во
Затирка	CG2WA Mapei Ultracolor Plus 132	(a+b)/ab·шов·t·1,6	3,0 кг
Затирка	CG2WA	(a+b)/ab·шов·t·1,6	1,0 кг
Клей	C2 TE S1 Ceresit CM 17	1,5 кг/м²·мм, слой 5	298 кг (12 меш.)
Клей	C2 TE S1	1,5 кг/м²·мм, слой 5	108 кг (5 меш.)
Гидроизоляция	обмазочная, 2 слоя: пол, стены по периметру и зоны замачивания	по ТУ	21,5 м²
Демпф. лента	по периметру пола из плитки		27,1 м

1000 мм · печать 1:1

Изм.	Кол.уч	Лист	№ док.	Подп.	Дата
Разраб.		Кырлан А.С.			18.10.26
Пров.					
ГИП					
Н. контр.					
Утв.					

ГД-2026-009-АИ

Квартира 103 м²

Общая площадь 100,72* м² · * размеры со скана, не замерены (реестр — л. 6, К-1)

Дизайн-проект интерьера

Стадия	Лист	Листов
РП	35	96

Раскладка плитки. Планы полов

М 1:20

Кырлан Александр Сергеевич

выпуск 18.10.2026 № 53dc234b8d · стр. 43 из 135

Раскладка плитки. Прихожая-холл

Раскладка от чистовых размеров · размеры в мм · высоты фартука от чистого пола

ПРЕДВАРИТЕЛЬНО · не для производства работ · открыто пунктов: 4 (реестр — л. 6)

Фрагмент 1. Прихожая-холл (пом. 4). Пол 600×1200, шов 2 мм, М 1:20

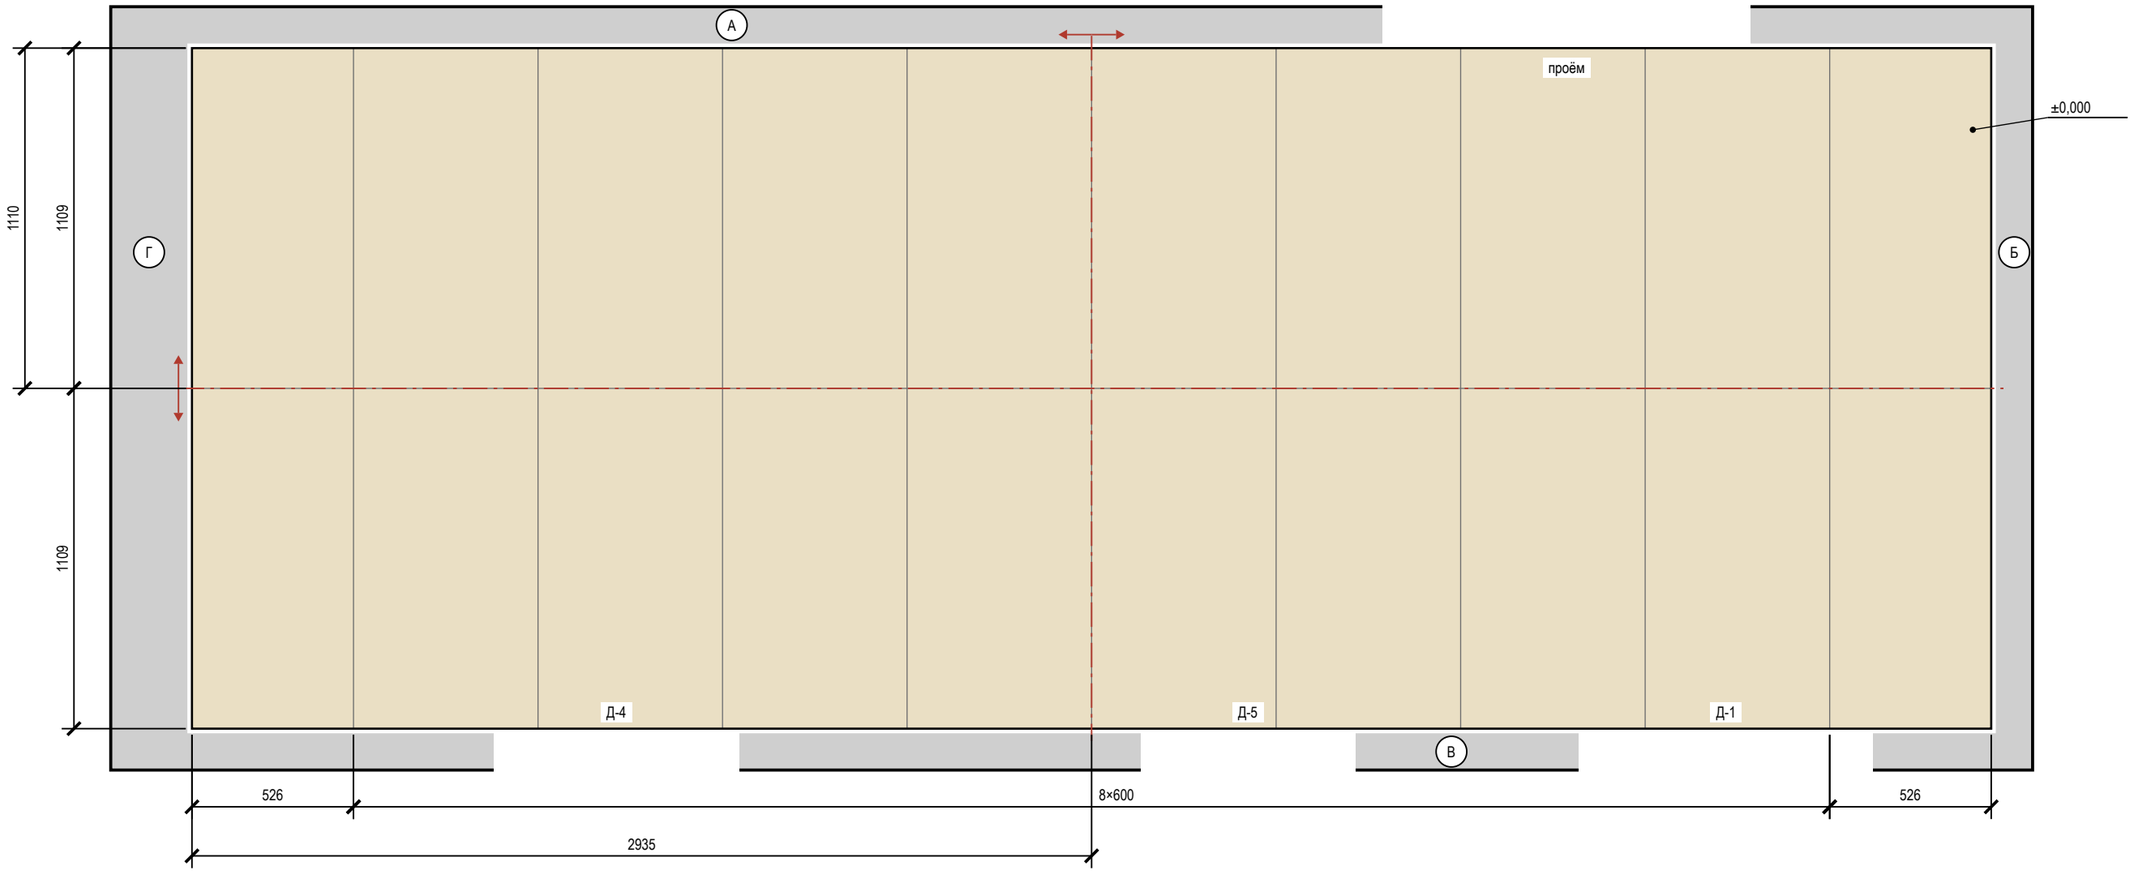

Условные обозначения

- плитка целая; тонкая линия — шов
- плитка с подрезкой (размер — на цепочке)
- ось старта; стрелки — направление укладки
- отметка чистого пола на полке выноски, м
- (А) обозначение стены А–Г (как на развёртках)

Подсчёт плитки

Поверхность	Формат	S, м²	Целых	Подр.	С запасом
Прихожая-холл, пол	600×1200	12,91	0	20	22

Примечания

1. Прихожая-холл: керамогранит 600×1200, длинная сторона — вдоль стен Б и Г, шов 2 мм, прямая раскладка от центра. Стены окрашены: раскладка от чистового контура минус штукатурка и шпаклёвка 15 мм на сторону (принято); подрезки 526 / 1109 мм, срез — под плинтус.
2. Прихожая-холл: деформационный зазор по периметру 8–10 мм под плинтусом; в проёмах — стык с соседним покрытием по оси полотна двери. Клей С2 TE S1, затирка CG2WA.
3. Клей, затирка и итог по форматам — в ведомостях листа «Раскладка плитки. Планы полов».

Допущения и предложения на листе

Основа листа: размеры сняты со скана обмерного плана KV design (см): часть подписей не читается, помещения выровнены по читаемым размерам; контрольный обмер не выполнен (К-1); высота потолка 2650 мм принята по отметкам обмера (Н = 2,50…2,66 м, ригель 2,28 м) — уточнить при обмере (К-2); толщины стен 300 / 120 мм приняты, межквартирная стена и колонны — по скану, не замерены (К-1); разрешённая мощность 15 кВт принята по типовым ТУ; при объединении двух квартир — переоформление ТУ (К-4).
Знак «**» — предложение проектировщика, заказчиком не утверждено (согласовать с заказчиком): записи в реестре нет: плинтус пом. 4 — артикул изделия не выбран: позиция описана характеристиками («аналог по характеристикам»), артикул выбирается при закупке.
См. лист открытых вопросов (лист 6, записи К-1, К-2, К-4).

1000 мм · печать 1:1

Изм.	Кол.уч	Лист	№ док.	Подп.	Дата
Разраб.		Кырлан А.С.			18.10.26
Пров.					
ГИП					
Н. контр.					
Утв.					

ГД-2026-009-АИ

Квартира 103 м²

Общая площадь 100,72* м² · * размеры со скана, не замерены (реестр — л. 6, К-1)

Дизайн-проект интерьера

Стадия	Лист	Листов
РП	36	96

Раскладка плитки. Прихожая-холл

М 1:20

Кырлан Александр Сергеевич

выпуск 18.10.2026 № 53dc234b8d · стр. 44 из 135

Раскладка плитки. Ванная. Развёртки стен

ПРЕДВАРИТЕЛЬНО · не для производства работ · открыто пунктов: 4 (реестр — л. 6)

Пом. 6 · вид изнутри помещения · размеры в мм · высоты от чистого пола, отметки от ±0,000

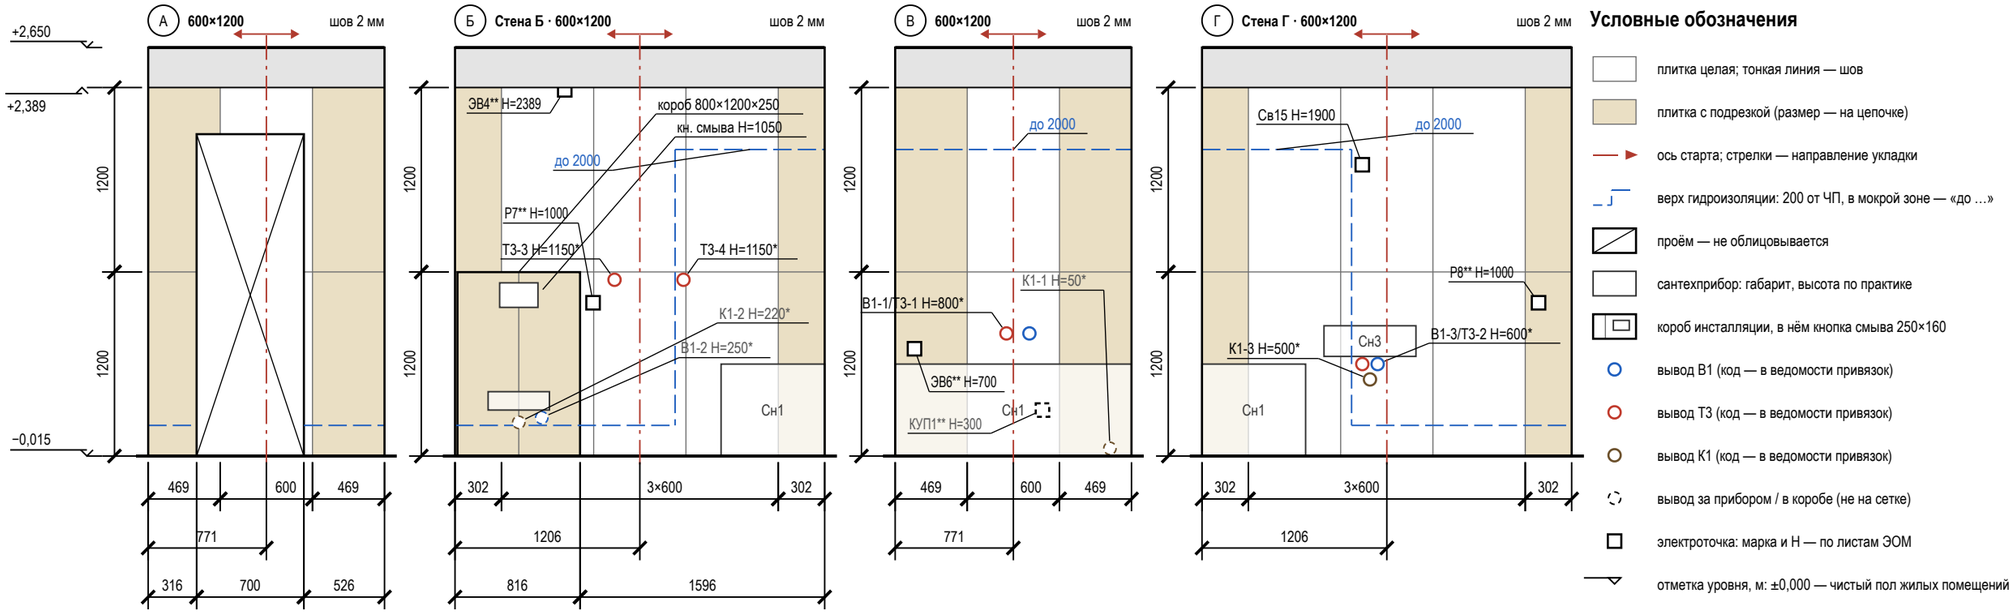

Условные обозначения

- плитка целая; тонкая линия — шов
- плитка с подрезкой (размер — на цепочке)
- ось старта; стрелки — направление укладки
- верх гидроизоляции: 200 от ЧП, в мокрой зоне — «до …»
- проём — не облицовывается
- сантехприбор: габарит, высота по практике
- короб инсталляции, в нём кнопка смыва 250×160
- вывод В1 (код — в ведомости привязок)
- вывод Т3 (код — в ведомости привязок)
- вывод К1 (код — в ведомости привязок)
- вывод за прибором / в коробе (не на сетке)
- электроточка: марка и Н — по листам ЭОМ
- отметка уровня, м: ±0,000 — чистый пол жилых помещений
- низ потолка; серая полоса — стена без плитки
- (А) обозначение стены А–Г (как на развёртках)

Подсчёт плитки по стенам и коробу

Поверхность	L × H, мм	S, м²	Целых	Подр.	С запасом	Подрезки: край / верх, мм
стена А	1542 × 2404	2,35	0	6	7	469 / 469; целый ряд
стена Б	2412 × 2404	4,95	5	5	11	302 / 302; целый ряд
короб (ст. Б)	800×1200×250	1,76	0	6	7	лицо 399 / 399; бок. 250
стена В	1542 × 2404	3,82	2	4	7	469 / 469; целый ряд
стена Г	2412 × 2404	5,91	6	4	11	302 / 302; целый ряд
Итого		**18,80**	**13**	**25**	**43**	

Сдвиг точек под раскладку

Точка (ВК, ЭОМ)	Стена	Проект: от угла / Н	Под раскладку: от угла / Н	Сдвиг, мм
Т3-3	Б	1041 / 1150	905 / 1150	−136 на шов
Т3-4	Б	1491 / 1150	1507 / 1150	+16 на шов
ЭВ4**	Б	716 / 2389	604 / 2403	−112 в центр плитки; Н +14
В1-1/Т3-1	В	801 / 800	771 / 800	−30 в центр плитки
ЭВ6**	В	126 / 700	169 / 700	+43 в центр плитки
В1-3/Т3-2, К1-3	Г	1096 / 600, 500	1206 / 600, 500	+110 в центр плитки
Р8**	Г	2196 / 1000	2109 / 1000	−87 на шов
Св15	Г	1046 / 1900	905 / 1900	−141 на шов

Примечания

1. Вид изнутри, стены по часовой стрелке А → Г. Высоты — от чистого пола (−0,015), отметки от ±0,000. Раскладка от чистовых размеров (штукатурка 10 + клей 5 + плитка 9 мм), подрезки чистые; старт — от оси стены, ряды от пола целыми.
2. Верх плитки +2,389, потолок +2,650, зазор 261 мм: потолок ГКЛ опустить до +2,392 (шов 3 мм, герметик) — согласовать с монтажником ГКЛ; иначе профиль-окантовка, полосу окрасить в цвет потолка. Подрезной ряд 256 мм не делать.
3. Точки из таблицы сдвигов переносятся до черновой разводки: смеситель — по оси пары В1 + Т3; вывод на оси прибора — вместе с прибором, иначе старт раскладки — на ось прибора.
4. Выводы — по «Плану выводов сантехники», электроточки — по ЭОМ, «*» — высота по практике; за приборами и в коробе (В1-2, К1-2, К1-1, КУП1**) — штриховым кольцом.
5. Гидроизоляция: 200 мм от ЧП по периметру; над ванной — до 2000 и 300 мм за борт (СП 29.13330.2011, п. 7.2 — на высоту замачивания); углы — лентой; акт скрытых работ, пролив.
6. Короб 800×1200×250: лицо 399 / 399 мм от оси кнопки смыва, боковины, полка; углы — запил 45° или профиль; за коробом плитку не кладут.
7. Между коробом и углом полоса 16 мм — довести короб до угла.

Допущения и предложения на листе

Основа листа: размеры сняты со скана обмерного плана KV design (см): часть подписей не читается, помещения выровнены по читаемым размерам; контрольный обмер не выполнен (К-1); высота потолка 2650 мм принята по отметкам обмера (Н = 2,50…2,66 м, ригель 2,28 м) — уточнить при обмере (К-2); толщины стен 300 / 120 мм приняты, межквартирная стена и колонны — по скану, не замерены (К-1); разрешённая мощность 15 кВт принята по типовым ТУ; при объединении двух квартир — переоформление ТУ (К-4).

Знак «**» — предложение проектировщика, заказчиком не утверждено (согласовать с заказчиком): записи в реестре нет: Р7, Р8 — по образцу: Р7, Р8 и Р33 на высоте 1000 мм — верхний предел нормы (ПУЭ, п. 6.6.30, не выше 1 м); флаг решения снят; ЭВ4, КУП1 — по образцу: Добавлены выводы к вентиляторам: ЭВ4 (ВР1, ванная) и ЭВ5 (ВР3, санузел 2) — группа 3, высота 2389 мм, включение с основным светом, таймер выбега в вентиляторе; и коробки уравнивания потенциалов КУП1 (ванная) и КУП2 (санузел 2) — высота 300 мм, у входа, вне зон 0–2, проводник от шины РЕ щита ЩК, сече; ЭВ6 — по образцу: Добавлены электрические полотенцесушители IP44: П10 в ванной (480 мм, низ 900 мм) и П13 в санузле 2 (400 мм, низ 900 мм), выводы ЭВ6 и ЭВ7; мощность группы 13 — 2,4 кВт вместо 1,8 кВт.

См. лист открытых вопросов (лист 6, записи К-1, К-2, К-4).

1000 мм · печать 1:1

Изм.	Кол.уч	Лист	№ док.	Подп.	Дата
Разраб.		Кырлан А.С.			18.10.26
Пров.					
ГИП					
Н. контр.					
Утв.					

ГД-2026-009-АИ

Квартира 103 м²

Общая площадь 100,72* м² · * размеры со скана, не замерены (реестр — л. 6, К-1)

Дизайн-проект интерьера

Стадия	Лист	Листов
РП	37	96

Раскладка плитки. Ванная. Развёртки стен

М 1:40

Кырлан Александр Сергеевич

выпуск 18.10.2026 № 53dc234b8d · стр. 45 из 135

Раскладка плитки. Ванная мастер. Развёртки стен

Пом. 11 · вид изнутри помещения · размеры в мм · высоты от чистого пола, отметки от ±0,000

ПРЕДВАРИТЕЛЬНО · не для производства работ · открыто пунктов: 4 (реестр — л. 6)

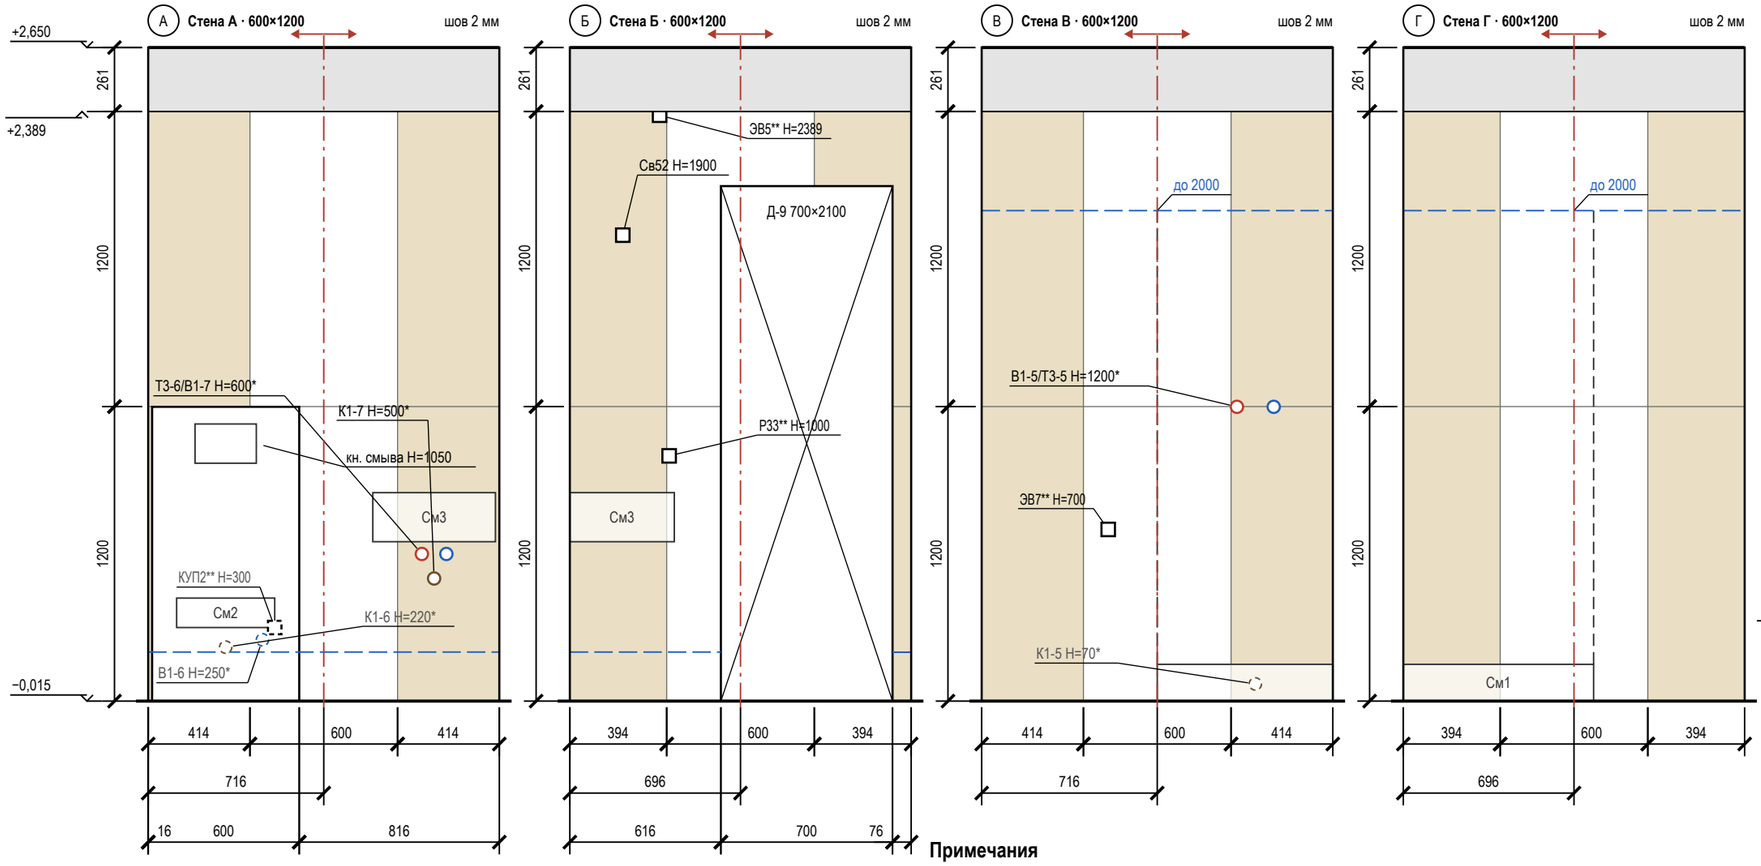

Условные обозначения

- плитка целая; тонкая линия — шов
- плитка с подрезкой (размер — на цепочке)
- ось старта; стрелки — направление укладки
- верх гидроизоляции: 200 от ЧП, в мокрой зоне — «до …»
- проём — не облицовывается
- сантехприбор: габарит, высота по практике
- граница душевой зоны (ограждение)
- короб инсталляции, в нём кнопка смыва 250×160
- вывод В1 (код — в ведомости привязок)
- вывод Т3 (код — в ведомости привязок)
- вывод К1 (код — в ведомости привязок)
- вывод за прибором / в коробе (не на сетке)
- электроточка: марка и Н — по листам ЭОМ
- отметка уровня, м: ±0,000 — чистый пол жилых помещений
- низ потолка; серая полоса — стена без плитки
- (А) обозначение стены А–Г (как на развёртках)

Примечания

1. Вид изнутри, стены по часовой стрелке А → Г. Высоты — от чистого пола (−0,015), отметки — от ±0,000. Раскладка от чистовых размеров (штукатурка 10 + клей 5 + плитка 9 мм), подрезки чистые; старт — от оси стены, ряды от пола целыми.
2. Верх плитки +2,389, потолок +2,650, зазор 261 мм: потолок ГКЛ опустить до +2,392 (шов 3 мм, герметик) — согласовать с монтажником ГКЛ; иначе профиль-окантовка, полосу окрасить в цвет потолка. Подрезной ряд 256 мм не делать.
3. Точки из таблицы сдвигов переносятся до черновой разводки: смеситель — по оси пары В1 + Т3; вывод на оси прибора — вместе с прибором, иначе старт раскладки — на ось прибора.
4. Выводы — по «Плану выводов сантехники», электроточки — по ЭОМ, «*» — высота по практике; за приборами и в коробе (В1-6, К1-6, КУП2**, К1-5) — штриховым кольцом.
5. Гидроизоляция: 200 мм от ЧП по периметру; у душа — до 2000 и 500 мм за поддон (СП 29.13330.2011, п. 7.2 — на высоту замачивания); углы — лентой; акт скрытых работ, пролив.
6. Короб 600×1200×250: лицо 600 мм от оси кнопки смыва, боковины, полка; углы — запил 45° или профиль; за коробом плитку не кладут.
7. Между коробом и углом полоса 16 мм — довести короб до угла.

Подсчёт плитки по стенам и коробу

Поверхность	L × H, мм	S, м²	Целых	Подр.	С запасом	Подрезки: край / верх, мм
стена А	1432 × 2404	2,84	1	5	7	414 / 414; целый ряд
короб (ст. А)	600×1200×250	1,47	1	3	5	лицо 600; бок. 250
стена Б	1392 × 2404	1,99	0	6	7	394 / 394; целый ряд
стена В	1432 × 2404	3,56	2	4	7	414 / 414; целый ряд
стена Г	1392 × 2404	3,46	2	4	7	394 / 394; целый ряд
Итого		**13,32**	**6**	**22**	**33**	

Сдвиг точек под раскладку

Точка (ВК, ЭОМ)	Стена	Проект: от угла / Н	Под раскладку: от угла / Н	Сдвиг, мм
Т3-6/В1-7, К1-7	А	1166 / 600, 500	1017 / 600, 500	−149 на шов
Св52	Б	216 / 1900	94 / 1900	−122 в центр плитки
ЭВ5**	Б	366 / 2389	395 / 2343	+29 на шов; Н −46
В1-5/Т3-5	В	1116 / 1200	1017 / 1141	−99 на шов; Н −59
ЭВ7**	В	516 / 700	415 / 700	−101 на шов

Допущения и предложения на листе

Основа листа: размеры сняты со скана обмерного плана KV design (см): часть подписей не читается, помещения выровнены по читаемым размерам; контрольный обмер не выполнен (К-1); высота потолка 2650 мм принята по отметкам обмера (Н = 2,50…2,66 м, ригель 2,28 м) — уточнить при обмере (К-2); толщины стен 300 / 120 мм приняты, межквартирная стена и колонны — по скану, не замерены (К-1); разрешённая мощность 15 кВт принята по типовым ТУ; при объединении двух квартир — переоформление ТУ (К-4).

Знак «**» — предложение проектировщика, заказчиком не утверждено (согласовать с заказчиком): записи в реестре нет: Р33 — по образцу: Розетка Р33 на высоте 1100 мм, вне шва плитки; ЭВ5, КУП2 — по образцу: Добавлены выводы к вентиляторам: ЭВ4 (ВР1, ванная) и ЭВ5 (ВР3, санузел 2) — группа 3, высота 2389 мм, включение с основным светом, таймер выбега в вентиляторе; и коробки уравнивания потенциалов КУП1 (ванная) и КУП2 (санузел 2) — высота 300 мм, у входа, вне зон 0–2, проводник от шины РЕ щита ЩК, сече; ЭВ7 — по образцу: Добавлены электрические полотенцесушители IP44: П10 в ванной (480 мм, низ 900 мм) и П13 в санузле 2 (400 мм, низ 900 мм), выводы ЭВ6 и ЭВ7; мощность группы 13 — 2,4 кВт вместо 1,8 кВт.

См. лист открытых вопросов (лист 6, записи К-1, К-2, К-4).

1000 мм · печать 1:1

						ГД-2026-009-АИ	
						Квартира 103 м²	
						Общая площадь 100,72* м² · * размеры со скана, не замерены (реестр — л. 6, К-1)	
Изм.	Кол.уч	Лист	№ док.	Подп.	Дата		
Разраб.		Кырлан А.С.			18.10.26	Дизайн-проект интерьера	Стадия: РП; Лист: 38; Листов: 96
Пров.							
ГИП							
Н. контр.						**Раскладка плитки. Ванная мастер. Развёртки стен** М 1:25	**Кырлан Александр Сергеевич**
Утв.							

выпуск 18.10.2026 № 53dc234b8d · стр. 46 из 135

07

Полы и отделка

Кырлан Александр Сергеевич

выпуск 18.10.2026 · № 53dc234b8d · стр. 47 из 135

План полов

Покрытия, направление укладки, отметки чистого пола, стыки · размеры в мм · отметки в м

ПРЕДВАРИТЕЛЬНО · не для производства работ · открыто пунктов: 4 (реестр — л. 6)

Условные обозначения

- тип 1 — инженерная доска, линии — вдоль доски
- тип 2 — инженерная доска, линии — вдоль доски
- тип 3 — керамогранит 600×1200, сетка — формат плитки
- тип 4 — инженерная доска, линии — вдоль доски
- тип 5 — керамогранит 600×1200, сетка — формат плитки
- 1 — номер типа пола (экспликация полов)
- схема пола, без масштаба: плита — штриховка, стяжка — точки, звукоизоляция — зигзаг, гидроизоляция — утолщённая линия с заведением на стену
- направление укладки (длинная сторона доски)
- отметка чистого пола, м
- стык в проёме: без порога (б/п)
- стык в проёме: решение не задано
- стык в проёме: порог
- СТ1 — марка стыка (ведомость стыков)
- стояк: К1 — канализация, В1 ХВС, Т3 — ГВС
- 1 — номер помещения, площадь м²

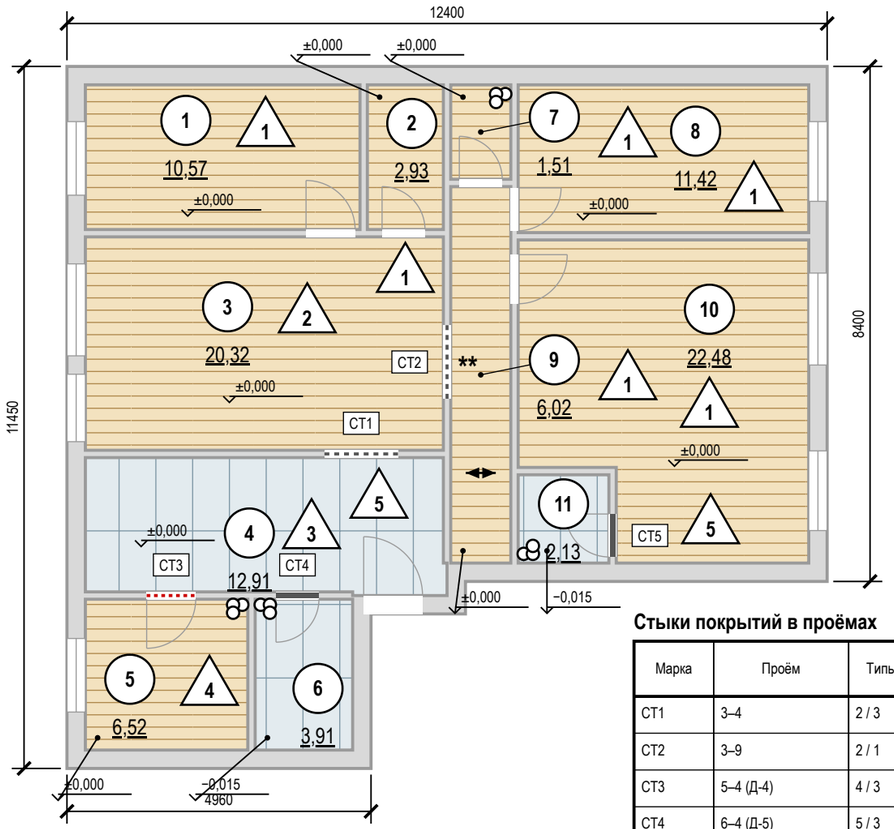

Стыки покрытий в проёмах

Марка	Проём	Типы пола	Отметки ЧП	Решение
СТ1	3–4	2 / 3	±0,000 / ±0,000	б/п
СТ2	3–9	2 / 1	±0,000 / ±0,000	б/п
СТ3	5–4 (Д-4)	4 / 3	±0,000 / ±0,000	не задано
СТ4	6–4 (Д-5)	5 / 3	−0,015 / ±0,000	порог h=15 мм
СТ5	11–10 (Д-9)	5 / 1	−0,015 / ±0,000	порог h=15 мм

Экспликация полов

Номер помещения	Тип пола	Схема пола	Данные элементов пола (наименование, толщина, основание), мм	Площадь, м²
1, 2, 7, 8, 9, 10	1		Инженерная доска на клею — 14 Стяжка ЦПС М200 — 50 Плита перекрытия Всего 64 мм; ЧП ±0,000, верх плиты −0,064	54,93
3	2		Инженерная доска дуб на клею — 14 Клей паркетный МС-полимерный — 1 Стяжка ЦПС М300 (В22,5), фибра, по звукоизоляции — 55 Звукоизоляция — минплита 110 кг/м³ 20 Засыпка керамзитовая фр. 0–5, уплотнённая — 80 Плита перекрытия монолитная Всего 170 мм; ЧП ±0,000, верх плиты −0,170	20,32
4	3		Керамогранит на клею С2 TE S1 — 14 Стяжка ЦПС М200 — 50 Плита перекрытия Всего 64 мм; ЧП ±0,000, верх плиты −0,064	12,91
5	4		Инженерная доска дуб на клею — 14 Клей паркетный МС-полимерный — 1 Гидроизоляция полиуретановая, 2 слоя (зона мойки и острова) — 2 Стяжка ЦПС М300 (В22,5), фибра, по звукоизоляции — 53 Звукоизоляция — минплита 110 кг/м³ 20 Засыпка керамзитовая фр. 0–5, уплотнённая — 80 Плита перекрытия монолитная Всего 170 мм; ЧП ±0,000, верх плиты −0,170	6,52
6, 11	5		Керамогранит на клею С2 TE S1 — 14 Гидроизоляция обмазочная, 2 слоя, с заведением на стены 200 мм — 2 Стяжка ЦПС М200 — 33 Плита перекрытия Всего 49 мм; ЧП −0,015, верх плиты −0,064	6,04
			Итого	**100,72**

Отметки по высоте

- **±0,000** — чистый пол пом. 1–5, 7–10; отсчёт высот
- **−0,015** — чистый пол пом. 6, 11, ниже на 15 мм
- **плита*** — верх плиты разный: −0,064, −0,170 (задание на обмер)
- **сущ. пол** — снимается до плиты; не замерен (задание на обмер)

Допущения и предложения на листе

Основа листа: размеры сняты со скана обмерного плана KV design (см): часть подписей не читается, помещения выровнены по читаемым размерам; контрольный обмер не выполнен (К-1); высота потолка 2650 мм принята по отметкам обмера (Н = 2,50…2,66 м, ригель 2,28 м) — уточнить при обмере (К-2); толщины стен 300 / 120 мм приняты, межквартирная стена и колонны — по скану, не замерены (К-1); разрешённая мощность 15 кВт принята по типовым ТУ; при объединении двух квартир — переоформление ТУ (К-4).

Знак «**» — предложение проектировщика, заказчиком не утверждено (согласовать с заказчиком): К-5: дверь пом. 3 (стена Б) — проём в межквартирной стене — объединение квартир, предложение до техзаключения; записи в реестре нет: плинтус пом. 1–5, 7–10, акцент пом. 3, фартук пом. 5 — артикул изделия не выбран: позиция описана характеристиками («аналог по характеристикам»), артикул выбирается при закупке.

Примечания

См. лист открытых вопросов (лист 6, записи К-1, К-2, К-4, К-5).

1. За отметку ±0,000 принят чистый пол, не существующий (блок отметок). Площади — по чистым размерам помещений, м²; размеры — в мм.
2. Стык разнотипных покрытий — по оси дверного полотна (под полотном в закрытом положении); решение стыка — по ведомости стыков.
3. Пол санузлов ниже смежных помещений на 15 мм; гидроизоляция по стяжке с заведением на стены не менее 200 мм (СП 29.13330.2011, п. 7.2), до облицовки — тест проливом и акт скрытых работ.
4. Трубопроводы в конструкции пола не прокладываются: пирог пола 49–170 мм не вмещает выпуски канализации с уклоном — выпуски К1 ведутся по стенам над чистым полом в коробах (лист 31).
5. Штучные покрытия (инженерная доска): направление — по стрелке; влажность основания по СМ не более 2,0 % (по ТУ изготовителя).
6. Ровность основания — просвет под 2-метровой рейкой не более 2 мм: пом. 1, 2, 3, 5, 7, 8, 9, 10 (инженерная доска), пом. 4, 6, 11 (керамогранит); проверить до укладки покрытия (СП 71.13330.2017, табл. 8.5).
7. Плавающая стяжка по звукоизоляции: демпферная (кромочная) лента по контуру помещения, у стояков и колонн — до верха чистого пола (СП 51.13330.2011, п. 9.11); плинтус крепится только к стене.
8. Сетка на плитке — условная, в размер формата; точка старта и раскладка — по листу раскладки плитки.
9. Пироги полов — по экспликации полов: слои сверху вниз, толщины в мм; гидроизоляция мокрых зон — в пироге и в ведомости отделки; схема пола — без масштаба.

1000 мм · печать 1:1

Изм.	Кол.уч	Лист	№ док.	Подп.	Дата
Разраб.		Кырлан А.С.			18.10.26
Пров.					
ГИП					
Н. контр.					
Утв.					

ГД-2026-009-АИ

Квартира 103 м²

Общая площадь 100,72* м² · * размеры со скана, не замерены (реестр — л. 6, К-1)

Дизайн-проект интерьера

Стадия	Лист	Листов
РП	39	96

План полов

М 1:100

Кырлан Александр Сергеевич

выпуск 18.10.2026 № 53dc234b8d · стр. 48 из 135

Ведомость отделки помещений. Лист 1 из 2

ПРЕДВАРИТЕЛЬНО · не для производства работ · открыто пунктов: 4 (реестр — л. 6)

Потолки, стены, низ стен, полы · площади в м², длины в м · отметки в м

Ведомость отделки помещений (форма 1 прил. А ГОСТ 21.501-2018). Лист 1 из 2

№	Наименование помещения	Потолок			Стены и перегородки			Низ стен (плинтус)			Пол		Примечание
		Вид отделки	Код цвета	S, м²	Вид отделки	Код цвета	S, м²	Вид отделки	Код цвета	L, м	Вид отделки	S, м²	
1	Кабинет-библиотека 10,57 м²	Окраска, Tikkurila Anti-Reflex 2, глубокоматовая, 2 слоя, подготовка Q3	NCS S 0502-Y	10,57	Окраска, Farrow & Ball Modern Emulsion, матовая, 2 слоя, подготовка Q3 Акцент — стена А: окраска, Farrow & Ball Modern Emulsion, матовая, 2 слоя, подготовка Q3	Farrow & Ball No. 291 Farrow & Ball No. 289	20,83 11,87	Плинтус МДФ h=80 мм, аналог: МДФ под покраску 80×16	Farrow & Ball No. 291	12,9	Инженерная доска, 1167-4250, 2100×127 мм, на клею; тип 1, отм. ЧП ±0,000	10,57	Н стен 2650 (до потолка); плинтус в цвет: стены
2	Кладовая 2,93 м²	Окраска, Tikkurila Anti-Reflex 2, глубокоматовая, 2 слоя, подготовка Q3	NCS S 0502-Y	2,93	Окраска, Tikkurila Harmony, матовая, 2 слоя, подготовка Q3	NCS S 0502-Y	17,61	Плинтус МДФ h=80 мм, аналог: МДФ под покраску 80×16	NCS S 0502-Y	6,5	Инженерная доска, 1167-4250, 2100×127 мм, на клею; тип 1, отм. ЧП ±0,000	2,93	Н стен 2650 (до потолка); плинтус в цвет: стены
3	Гостиная-столовая 20,32 м²	Окраска, Tikkurila Anti-Reflex 2, глубокоматовая, 2 слоя, подготовка Q3	Farrow & Ball No. 291	20,32	Окраска, Tikkurila Optiva 5 Matt, матовая, 2 слоя, подготовка К3 Акцент — стена А: окраска, Tikkurila Optiva 5 Matt, матовая, 3 слоя, подготовка К3	Farrow & Ball No. 291 Farrow & Ball No. 255	24,85 12,33	Плинтус МДФ h=80 мм, аналог: МДФ под окраску 80×16 мм	Farrow & Ball No. 291	14,7	Инженерная доска, 1167-4250, 2100×127 мм, на клею; тип 2, отм. ЧП ±0,000	20,32	Н стен 2650 (до потолка); колерується в код стен, но по эмали на МДФ: сличать отдельным выкрасом на своей подложке (выкрас № 10); плинтус в цвет: стены
4	Прихожая-холл 12,91 м²	Окраска, Tikkurila Anti-Reflex 2, глубокоматовая, 2 слоя, подготовка Q3	NCS S 0502-Y	12,91	Окраска, Farrow & Ball Modern Emulsion, матовая, 2 слоя, подготовка Q3	Farrow & Ball No. 291	35,51	Плинтус МДФ h=80 мм, аналог: МДФ под покраску 80×16	Farrow & Ball No. 291	12,6	Керамогранит, A8UZ, 600×1200×9 мм; тип 3, отм. ЧП ±0,000	12,91	Н стен 2650 (до потолка); матовая моющаяся, класс 1 EN 13300 — осознанно вместо полуматовой; плинтус в цвет: стены
5	Кухня 6,52 м²	Окраска, Tikkurila Luja 7, матовая, 2 слоя, подготовка Q3	Farrow & Ball No. 291	6,52	Окраска, Tikkurila Luja 7, полуматовая, 2 слоя, подготовка К3 Фартук кухни (стена Б, В): облицовка керамогранитом, аналог: керамогранит матовый, тон F497, 600×600×9 мм, клей C2 TE S1, затирка CG2WA	Farrow & Ball No. 291 #F1F1EC	21,86 1,68	Плинтус МДФ h=80 мм, аналог: МДФ под окраску 80×16 мм	Farrow & Ball No. 291	9,4	Инженерная доска, 1167-4250, 2100×127 мм, на клею; тип 4, отм. ЧП ±0,000	6,52	Н стен 2650 (до потолка); влагостойкая полуматовая окраска (класс мокрого истирания 1 по EN 13300); категория К3 по СП 71.13330.2017, табл. 7.5; по ГКЛ каркаса П113, влагостойкая окраска; Q3 колерується в код стен, но по эмали на МДФ: сличать отдельным выкрасом на своей подложке (выкрас № 10); плинтус в цвет: стены
6	Ванная 3,91 м²	Окраска, Tikkurila Luja 7, матовая, 2 слоя, подготовка Q3	NCS S 0502-Y	3,91	Облицовка плиткой, A8UZ, 600×1200×9 мм, клей C2 TE S1, затирка CG2WA	Atlas Concorde A8UZ	18,00	нет			Керамогранит, A8UZ, 600×1200×9 мм; тип 5, отм. ЧП −0,015	3,91	Н стен 2665 (до потолка); гидроизоляция обмазочная, 2 слоя, с заведением на стены 200 мм (по пирогу пола); тест проливом и акт скрытых работ
7	Постирочная 1,51 м²	Окраска, Tikkurila Anti-Reflex 2, глубокоматовая, 2 слоя, подготовка Q3	NCS S 0502-Y	1,51	Окраска, Tikkurila Harmony, матовая, 2 слоя, подготовка Q3	NCS S 0502-Y	11,89	Плинтус МДФ h=80 мм, аналог: МДФ под покраску 80×16	NCS S 0502-Y	4,3	Инженерная доска, 1167-4250, 2100×127 мм, на клею; тип 1, отм. ЧП ±0,000	1,51	Н стен 2650 (до потолка); плинтус в цвет: стены
8	Спальня 2 11,42 м²	Окраска, Tikkurila Anti-Reflex 2, глубокоматовая, 2 слоя, подготовка Q3	NCS S 0502-Y	11,42	Окраска, Farrow & Ball Modern Emulsion, матовая, 2 слоя, подготовка Q3 Акцент — стена А: окраска, Farrow & Ball Modern Emulsion, матовая, 2 слоя, подготовка Q3	Farrow & Ball No. 291 Farrow & Ball No. 289	21,85 12,56	Плинтус МДФ h=80 мм, аналог: МДФ под покраску 80×16	Farrow & Ball No. 291	13,6	Инженерная доска, 1167-4250, 2100×127 мм, на клею; тип 1, отм. ЧП ±0,000	11,42	Н стен 2650 (до потолка); плинтус в цвет: стены

Примечания

1. Ведомость продолжена на листе 2 из 2; итоги, сводка площадей и примечания — на последнем листе ведомости.

Допущения и предложения на листе

Основа листа: размеры сняты со скана обмерного плана KV design (см): часть подписей не читается, помещения выровнены по читаемым размерам; контрольный обмер не выполнен (К-1); высота потолка 2650 мм принята по отметкам обмера (Н = 2,50…2,66 м, ригель 2,28 м) — уточнить при обмере (К-2); толщины стен 300 / 120 мм приняты, межквартирная стена и колонны — по скану, не замерены (К-1); разрешённая мощность 15 кВт принята по типовым ТУ; при объединении двух квартир — переоформление ТУ (К-4).
Знак «**» — предложение проектировщика, заказчиком не утверждено (согласовать с заказчиком): записи в реестре нет: плинтус пом. 1–5, 7–10, акцент пом. 3, фартук пом. 5 — артикул изделия не выбран: позиция описана характеристиками («аналог по характеристикам»), артикул выбирается при закупке.
См. лист открытых вопросов (лист 6, записи К-1, К-2, К-4).

Изм.	Кол.уч	Лист	№ док.	Подп.	Дата
Разраб.		Кырлан А.С.			18.10.26
Пров.					
ГИП					
Н. контр.					
Утв.					

ГД-2026-009-АИ

Квартира 103 м²

Общая площадь 100,72* м² · * размеры со скана, не замерены (реестр — л. 6, К-1)

Дизайн-проект интерьера	Стадия	Лист	Листов
	РП	40	96

Ведомость отделки помещений. Лист 1 из 2

М б/м

Кырлан Александр Сергеевич

выпуск 18.10.2026 № 53dc234b8d · стр. 49 из 135

Ведомость отделки помещений. Лист 2 из 2

Потолки, стены, низ стен, полы · площади в м², длины в м · отметки в м

Ведомость отделки помещений (форма 1 прил. А ГОСТ 21.501-2018). Лист 2 из 2

№	Наименование помещения	Потолок			Стены и перегородки			Низ стен (плинтус)			Пол		Примечание
		Вид отделки	Код цвета	S, м²	Вид отделки	Код цвета	S, м²	Вид отделки	Код цвета	L, м	Вид отделки	S, м²	
9	Коридор 6,02 м²	Окраска, Tikkurila Anti-Reflex 2, глубокоматовая, 2 слоя, подготовка Q3	NCS S 0502-Y	6,02	Окраска, Farrow & Ball Modern Emulsion, матовая, 2 слоя, подготовка Q3	Farrow & Ball No. 291	30,60	Плинтус МДФ h=80 мм, аналог: МДФ под покраску 80×16	Farrow & Ball No. 291	10,8	Инженерная доска, 1167-4250, 2100×127 мм, на клею; тип 1, отм. ЧП ±0,000	6,02	Н стен 2650 (до потолка); матовая моющаяся, класс 1 EN 13300 — осознанно вместо полуматовой; плинтус в цвет: стены
10	Спальня мастер 22,48 м²	Окраска, Tikkurila Anti-Reflex 2, глубокоматовая, 2 слоя, подготовка Q3	NCS S 0502-Y	22,48	Окраска, Farrow & Ball Modern Emulsion, матовая, 2 слоя, подготовка Q3 Акцент — стена А: окраска, Farrow & Ball Modern Emulsion, матовая, 2 слоя, подготовка Q3	Farrow & Ball No. 291 Farrow & Ball No. 289	33,01 12,56	Плинтус МДФ h=80 мм, аналог: МДФ под покраску 80×16	Farrow & Ball No. 291	18,5	Инженерная доска, 1167-4250, 2100×127 мм, на клею; тип 1, отм. ЧП ±0,000	22,48	Н стен 2650 (до потолка); плинтус в цвет: стены
11	Ванная мастер 2,13 м²	Окраска, Tikkurila Luja 7, матовая, 2 слоя, подготовка Q3	NCS S 0502-Y	2,13	Облицовка плиткой, A8UZ, 600×1200×9 мм, клей C2 TE S1, затирка CG2WA	Atlas Concorde A8UZ	12,57	нет			Керамогранит, A8UZ, 600×1200×9 мм; тип 5, отм. ЧП −0,015	2,13	Н стен 2665 (до потолка); гидроизоляция обмазочная, 2 слоя, с заведением на стены 200 мм (по пирогу пола); тест проливом и акт скрытых работ
	Итого			**100,72**			**299,57**			**103,5**		**100,72**	

Сводка площадей по материалам отделки

Поверхность	Материал / код цвета	Серия	Площадь, м²
Потолок	NCS S 0502-Y	Anti-Reflex 2	67,84
Потолок	Farrow & Ball No. 291	Anti-Reflex 2	20,32
Потолок	Farrow & Ball No. 291	Luja 7	6,52
Потолок	NCS S 0502-Y	Luja 7	6,04
Стены	Farrow & Ball No. 291	Modern Emulsion	141,79
Стены	Farrow & Ball No. 289	Modern Emulsion	36,99
Стены	NCS S 0502-Y	Harmony	29,50
Стены	Farrow & Ball No. 291	Optiva 5 Matt	24,85
Стены	Farrow & Ball No. 255	Optiva 5 Matt	12,33
Стены	Farrow & Ball No. 291	Luja 7	21,86
Стены	облицовка плиткой 600×1200×9 мм, Atlas Concorde A8UZ	A8UZ	30,57
Фартук	облицовка керамогранитом, #F1F1EC	аналог: керамогранит матовый, тон F497	1,68

Допущения и предложения на листе

Основа листа: размеры сняты со скана обмерного плана KV design (см): часть подписей не читается, помещения выровнены по читаемым размерам; контрольный обмер не выполнен (К-1); высота потолка 2650 мм принята по отметкам обмера (Н = 2,50…2,66 м, ригель 2,28 м) — уточнить при обмере (К-2); толщины стен 300 / 120 мм приняты, межквартирная стена и колонны — по скану, не замерены (К-1); разрешённая мощность 15 кВт принята по типовым ТУ; при объединении двух квартир — переоформление ТУ (К-4).

Знак «**» — предложение проектировщика, заказчиком не утверждено (согласовать с заказчиком): записи в реестре нет: плинтус пом. 1–5, 7–10, акцент пом. 3, фартук пом. 5 — артикул изделия не выбран: позиция описана характеристиками («аналог по характеристикам»), артикул выбирается при закупке.

См. лист открытых вопросов (лист 6, записи К-1, К-2, К-4).

Примечания

1. Площади поверхностей — по чистым граням стен до отделки: стены = периметр × высоту от чистого пола помещения до низа потолка минус проёмы (облицовка плиткой — до верха облицовки); плинтус = периметр минус дверные проёмы; пол и потолок — по площади помещения. Количество плиток по раскладке. Площади помещений — с учётом всех частей помещения; откосы в площадь стен не входят.
2. Акцентные стены и фартук — отдельными строками, их площадь вычтена из основной отделки стен помещения; фартук — над нижними модулями кухни от столешницы до низа навесных шкафов, где шкафов нет — на 600 мм.
3. Плинтус — длина по периметру за вычетом дверных проёмов; примыкания к наличникам и встроенной мебели — по развёрткам.
4. Формат плитки — Ш×В×Т (ширина × высота в положении укладки × толщина), мм; на полу — вдоль стен А/В × вдоль стен Б/Г.
5. Коды цвета — по веерам производителей; колеровка каждой краски одной партией, проверка выкраса при свете D65 и при лампах проекта.
6. Уровни подготовки Q1–Q4 — система Knauf, не норма ГОСТ/СП; допуски поверхностей — по СП 71.13330.2017 (действующая редакция).
7. «аналог:» — изделие задано характеристиками, марку и артикул согласовать с заказчиком до закупки.
8. Плавающая стяжка по звукоизоляции: демпферная (кромочная) лента по контуру помещения и у стояков (СП 51.13330.2011, п. 9.11); плинтус крепится только к стене.

Изм.	Кол.уч	Лист	№ док.	Подп.	Дата	ГД-2026-009-АИ			
						Квартира 103 м²			
						Общая площадь 100,72* м² · * размеры со скана, не замерены (реестр — л. 6, К-1)			
Разраб.		Кырлан А.С.			18.10.26	Дизайн-проект интерьера	Стадия	Лист	Листов
Пров.							РП	41	96
ГИП									
						Ведомость отделки помещений. Лист 2 из 2	Кырлан Александр Сергеевич		
Н. контр.						М б/м			
Утв.									

выпуск 18.10.2026 № 53dc234b8d · стр. 50 из 135

Колерная карта

Цвета и материалы по помещениям · палитра проекта · лист 1 из 2

Колерная карта по помещениям

Помещение	Поверхность	Образец	Поз.	Система и код цвета	Производитель, линейка / материал, артикул	Блеск	Класс EN 13300	LRV	Площадь
1. Кабинет-библиотека 10,57 м²	стены		**K1**	Farrow & Ball No. 291	Farrow & Ball · Modern Emulsion	матовая	1	73	20,8 м²
	акцент А		**K2**	Farrow & Ball No. 289	Farrow & Ball · Modern Emulsion	матовая	1	13	11,9 м²
	потолок		**K3**	NCS S 0502-Y	Tikkurila · Anti-Reflex 2	глубокомат.	2	95	10,6 м²
	пол		**KM1**	по образцу	Coswick · Вековые традиции				10,6 м²
	плинтус		**K4**	Farrow & Ball No. 291	МДФ · в цвет Farrow & Ball			73	12,9 м
2. Кладовая 2,93 м²	стены		**K5**	NCS S 0502-Y	Tikkurila · Harmony	матовая	1	95	17,6 м²
	потолок		**K3**	NCS S 0502-Y	Tikkurila · Anti-Reflex 2	глубокомат.	2	95	2,9 м²
	пол		**KM1**	по образцу	Coswick · Вековые традиции				2,9 м²
	плинтус		**K6**	NCS S 0502-Y	МДФ · в цвет NCS			95	6,5 м
3. Гостиная-столовая 20,32 м²	стены		**K7**	Farrow & Ball No. 291	Tikkurila · Optiva 5 Matt	матовая	2	73	24,9 м²
	акцент А		**K8**	Farrow & Ball No. 255	Tikkurila · Optiva 5 Matt	матовая	2	7	12,3 м²
	потолок		**K9**	Farrow & Ball No. 291	Tikkurila · Anti-Reflex 2	глубокомат.	2	73	20,3 м²
	пол		**KM1**	по образцу	Coswick · Вековые традиции				20,3 м²
	плинтус		**K10**	Farrow & Ball No. 291	МДФ · в цвет Farrow & Ball	полуглянц.	2	73	14,7 м
4. Прихожая-холл 12,91 м²	стены		**K1**	Farrow & Ball No. 291	Farrow & Ball · Modern Emulsion	матовая	1	73	35,5 м²
	потолок		**K3**	NCS S 0502-Y	Tikkurila · Anti-Reflex 2	глубокомат.	2	95	12,9 м²
	пол		**K11**	Atlas Concorde A8UZ	Atlas Concorde · Marvel Travertine				12,9 м²
	плинтус		**K4**	Farrow & Ball No. 291	МДФ · в цвет Farrow & Ball			73	12,6 м
5. Кухня 6,52 м²	стены		**K12**	Farrow & Ball No. 291	Tikkurila · Luja 7	полуматов.	1	73	21,9 м²
	потолок		**K13**	Farrow & Ball No. 291	Tikkurila · Luja 7	матовая	1	73	6,5 м²
	пол		**KM1**	по образцу	Coswick · Вековые традиции				6,5 м²
	плинтус		**K10**	Farrow & Ball No. 291	МДФ · в цвет Farrow & Ball	полуглянц.	2	73	9,4 м
	фартук		**KM2**	тон Paper F497 (тёплый белый)	керамогранит · аналог по хар.				1,7 м²

Схема палитры проекта

Стиль: Мид-сенчури 65% + Ар-деко 35% · схема: complement

основной Farrow & Ball No. 291	основной NCS S 1005-Y20R	основной NCS S 0502-Y	второстепенный Farrow & Ball No. 298	второстепенный Farrow & Ball No. 289	второстепенный Farrow & Ball No. 255	акцентный NCS S 2050-Y20R	акцентный NCS S 3050-Y70R	акцентный NCS S 5030-B10G	акцентный NCS S 5040-B90G
School House White – тёплый меловой белый LRV 73 стены 1,3,4,5,8,9,10; плинтус 1,3,4,5,8,9,10; потолок 5,5; текстиль/декор 3	Светлый кремовый LRV 77 текстиль/декор 1,3,5,8,10	Белый с лёгкой желтизной LRV 95 потолок 1,2,4,6,7,8,9,10,11; стены 2,7; плинтус 2,7; текстиль/декор 1,8,10	Bancha – оливковый середины века LRV 14 текстиль/декор 3,10	Inchyra Blue — тёмный сине-серый LRV 13 акцент 1,8,10; текстиль/декор 1,8,10	Tanner's Brown – тёмный шоколад LRV 7 акцент 3; текстиль/декор 3	Горчичный LRV 42 текстиль/декор 1,8	Терракотовый / жжёный оранжевый LRV 18 текстиль/декор 1,8	Тил LRV 12 текстиль/декор 8	Изумрудный LRV 8 в отделке не применён

План 60/30/10

Окраска, факт — по площади стен, акцентов, потолков

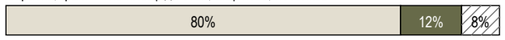

окрашено всего 398,6 м²; второстепенный тон несут мебель и текстиль

Условные обозначения

- **K1** Farrow & Ball No. 291 · School House White — тёплый меловой белый · Modern Emulsion · матовая · кл. 1
- **K2** Farrow & Ball No. 289 · Inchyra Blue — тёмный сине-серый · Modern Emulsion · матовая · кл. 1
- **K3** NCS S 0502-Y · Белый с лёгкой желтизной · Tikkurila Anti-Reflex 2 · глубокомат. · кл. 2
- **K4** Farrow & Ball No. 291 · School House White — тёплый меловой белый · МДФ
- **K5** NCS S 0502-Y · Белый с лёгкой желтизной · Tikkurila Harmony · матовая · кл. 1
- **K6** NCS S 0502-Y · Белый с лёгкой желтизной · МДФ
- **K7** Farrow & Ball No. 291 · School House White — тёплый меловой белый · Optiva 5 Matt · матовая · кл. 2
- **K8** Farrow & Ball No. 255 · Tanner's Brown — тёмный шоколад · Optiva 5 Matt · матовая · кл. 2
- дерево (доска, паркет, ламинат) — рисунок досок
- керамогранит, плитка, камень — сетка швов по формату
- HEX не задан — цвет только по коду и вееру
- **K9** Farrow & Ball No. 291 · School House White — тёплый меловой белый · Anti-Reflex 2 · глубокомат. · кл. 2
- **K10** Farrow & Ball No. 291 · School House White — тёплый меловой белый · МДФ · полуглянц. · кл. 2
- **K11** Atlas Concorde A8UZ · Marvel Travertine · Marvel Travertine
- **K12** Farrow & Ball No. 291 · School House White — тёплый меловой белый · Luja 7 · полуматов. · кл. 1
- **K13** Farrow & Ball No. 291 · School House White — тёплый меловой белый · Luja 7 · матовая · кл. 1
- **K14** NCS S 0502-Y · Белый с лёгкой желтизной · Tikkurila Luja 7 · матовая · кл. 1
- **KM1** инженерная доска · 1167-4250
- **KM2** аналог: керамогранит матовый, тон F497, 600×600×9 мм

К — позиция окраски (код + продукт + блеск), КМ — позиция материала, тон КМ — по описанию артикула, эталон — образец материала; ≈ LRV — расчёт по HEX, справочно

Допущения и предложения на листе

Основа листа: размеры сняты со скана обмерного плана KV design (см): часть подписей не читается, помещения выровнены по читаемым размерам; контрольный обмер не выполнен (К-1); высота потолка 2650 мм принята по отметкам обмера (Н = 2,50…2,66 м, ригель 2,28 м) — уточнить при обмере (К-2); толщины стен 300 / 120 мм приняты, межквартирная стена и колонны — по скану, не замерены (К-1); разрешённая мощность 15 кВт принята по типовым ТУ; при объединении двух квартир — переоформление ТУ (К-4).

Знак «**» — предложение проектировщика, заказчиком не утверждено (согласовать с заказчиком): записи в реестре нет: плинтус пом. 1–5, 7–10, акцент пом. 3, фартук пом. 5 — артикул изделия не выбран: позиция описана характеристиками («аналог по характеристикам»), артикул выбирается при закупке.

См. лист открытых вопросов (лист 6, записи К-1, К-2, К-4).

Примечания

1. Цвет утверждается только по выкрасу на объекте: формат от А3 до 1000×1000 мм на загрунтованном ГКЛ, в 2 слоя (как на стене), не на белой шпаклёвке; смотреть днём и при свете проекта своего помещения, рядом с образцами пола и фасадов. Подпись на обороте: код, бренд и веер, дата.
2. Колеровка машинная в колеровочном центре бренда; каждый код — за один проход, одной партией на весь объём. Колеровщику передаётся только система и код утверждённого веера; плашки и HEX на листе — ориентир, печать не является эталоном цвета.
3. Класс мокрого истирания — EN 13300 (ISO 11998); блеск — по ГОСТ 31975 (ISO 2813), геометрия 60°. LRV — пересчёт координаты L* каталога производителя (Y = ((L*+16)/116)³); «≈» — расчёт по HEX, справочно.
4. Площади поверхностей — тем же способом и с теми же цифрами, что в ведомости отделки (способ счёта — в общих указаниях); объём краски к заказу, фасовка и материалы КМ — в спецификации отделочных материалов.
5. Колерная карта на 2 листах: обозначения повторены на каждом, схема квартиры и палитра — на первом, перечень выкрасов — на последнем.

Изм.	Кол.уч	Лист	№ док.	Подп.	Дата
Разраб.		Кырлан А.С.			18.10.26
Пров.					
ГИП					
Н. контр.					
Утв.					

ГД-2026-009-АИ

Квартира 103 м²

Общая площадь 100,72* м² · * размеры со скана, не замерены (реестр — л. 6, К-1)

Дизайн-проект интерьера

Стадия	Лист	Листов
РП	42	96

Колерная карта

М б/м

Кырлан Александр Сергеевич

выпуск 18.10.2026 № 53dc234b8d · стр. 51 из 135

Колерная карта

Цвета и материалы по помещениям · выкрасы на согласование · лист 2 из 2

Колерная карта по помещениям (продолжение)

Помещение	Поверхность	Образец	Поз.	Система и код цвета	Производитель, линейка / материал, артикул	Блеск	Класс EN 13300	LRV	Площадь
6. Ванная 3,91 м²	стены		**K11**	Atlas Concorde A8UZ	Atlas Concorde · Marvel Travertine				18,0 м²
	потолок		**K14**	NCS S 0502-Y	Tikkurila · Luja 7	матовая	1	95	3,9 м²
	пол		**K11**	Atlas Concorde A8UZ	Atlas Concorde · Marvel Travertine				3,9 м²
7. Постирочная 1,51 м²	стены		**K5**	NCS S 0502-Y	Tikkurila · Harmony	матовая	1	95	11,9 м²
	потолок		**K3**	NCS S 0502-Y	Tikkurila · Anti-Reflex 2	глубокомат.	2	95	1,5 м²
	пол		**KM1**	по образцу	Coswick · Вековые традиции				1,5 м²
	плинтус		**K6**	NCS S 0502-Y	МДФ · в цвет NCS			95	4,3 м
8. Спальня 2 11,42 м²	стены		**K1**	Farrow & Ball No. 291	Farrow & Ball · Modern Emulsion	матовая	1	73	21,8 м²
	акцент А		**K2**	Farrow & Ball No. 289	Farrow & Ball · Modern Emulsion	матовая	1	13	12,6 м²
	потолок		**K3**	NCS S 0502-Y	Tikkurila · Anti-Reflex 2	глубокомат.	2	95	11,4 м²
	пол		**KM1**	по образцу	Coswick · Вековые традиции				11,4 м²
	плинтус		**K4**	Farrow & Ball No. 291	МДФ · в цвет Farrow & Ball			73	13,6 м
9. Коридор 6,02 м²	стены		**K1**	Farrow & Ball No. 291	Farrow & Ball · Modern Emulsion	матовая	1	73	30,6 м²
	потолок		**K3**	NCS S 0502-Y	Tikkurila · Anti-Reflex 2	глубокомат.	2	95	6,0 м²
	пол		**KM1**	по образцу	Coswick · Вековые традиции				6,0 м²
	плинтус		**K4**	Farrow & Ball No. 291	МДФ · в цвет Farrow & Ball			73	10,8 м
10. Спальня мастер 22,48 м²	стены		**K1**	Farrow & Ball No. 291	Farrow & Ball · Modern Emulsion	матовая	1	73	33,0 м²
	акцент А		**K2**	Farrow & Ball No. 289	Farrow & Ball · Modern Emulsion	матовая	1	13	12,6 м²
	потолок		**K3**	NCS S 0502-Y	Tikkurila · Anti-Reflex 2	глубокомат.	2	95	22,5 м²
	пол		**KM1**	по образцу	Coswick · Вековые традиции				22,5 м²
	плинтус		**K4**	Farrow & Ball No. 291	МДФ · в цвет Farrow & Ball			73	18,5 м
11. Ванная мастер 2,13 м²	стены		**K11**	Atlas Concorde A8UZ	Atlas Concorde · Marvel Travertine				12,6 м²
	потолок		**K14**	NCS S 0502-Y	Tikkurila · Luja 7	матовая	1	95	2,1 м²
	пол		**K11**	Atlas Concorde A8UZ	Atlas Concorde · Marvel Travertine				2,1 м²

Перечень выкрасов на согласование

№	Код	Бренд / веер	Пом. / стена	Подложка	Формат	Статус
1	No. 291	Farrow & Ball	1, 3, 4, 5, 8, 9, 10	ГКЛ, загрунтованный под эту краску; МДФ, загрунтованный под эмаль	600×1000; 300×600	к выполнению
2	No. 289	Farrow & Ball	1 А, 8 А, 10 А	ГКЛ, загрунтованный под эту краску	600×1000	к выполнению
3	S 0502-Y	NCS Tikkurila	1, 2, 4, 6, 7, 8, 9, 10, 11	ГКЛ, загрунтованный под эту краску; МДФ, загрунтованный под эмаль	600×1000; 300×600	к выполнению
4	No. 255	Farrow & Ball	3 А	ГКЛ, загрунтованный под эту краску	600×1000	к выполнению

Примечания

1. Цвет утверждается только по выкрасу на объекте: формат от А3 до 1000×1000 мм на загрунтованном ГКЛ, в 2 слоя (как на стене), не на белой шпаклёвке; смотреть днём и при свете проекта своего помещения, рядом с образцами пола и фасадов. Подпись на обороте: код, бренд и веер, дата.
2. Колеровка машинная в колеровочном центре бренда; каждый код — за один проход, одной партией на весь объём. Колеровщику передаётся только система и код утверждённого веера; плашки и HEX на листе — ориентир, печать не является эталоном цвета.
3. Класс мокрого истирания — EN 13300 (ISO 11998); блеск — по ГОСТ 31975 (ISO 2813), геометрия 60°. LRV — пересчёт координаты L* каталога производителя (Y = ((L*+16)/116)³); «≈» — расчёт по HEX, справочно.
4. Площади поверхностей — тем же способом и с теми же цифрами, что в ведомости отделки (способ счёта — в общих указаниях); объём краски к заказу, фасовка и материалы КМ — в спецификации отделочных материалов.
5. Перечень выкрасов составлен по кодам колерной карты; к основному тону стен добавить на выкрас 2 соседних тона того же веера (светлее и темнее), статус отмечать в графе «Статус» при согласовании.
6. Колерная карта на 2 листах: обозначения повторены на каждом, схема квартиры и палитра — на первом, перечень выкрасов — на последнем.

Условные обозначения

- **K1** Farrow & Ball No. 291 · School House White — тёплый меловой белый · Modern Emulsion · матовая · кл. 1
- **K2** Farrow & Ball No. 289 · Inchyra Blue — тёмный сине-серый · Modern Emulsion · матовая · кл. 1
- **K3** NCS S 0502-Y · Белый с лёгкой желтизной · Tikkurila Anti-Reflex 2 · глубокомат. · кл. 2
- **K4** Farrow & Ball No. 291 · School House White — тёплый меловой белый · МДФ
- **K5** NCS S 0502-Y · Белый с лёгкой желтизной · Tikkurila Harmony · матовая · кл. 1
- **K6** NCS S 0502-Y · Белый с лёгкой желтизной · МДФ
- **K7** Farrow & Ball No. 291 · School House White — тёплый меловой белый · Optiva 5 Matt · матовая · кл. 2
- **K8** Farrow & Ball No. 255 · Tanner's Brown — тёмный шоколад · Optiva 5 Matt · матовая · кл. 2
- **K9** Farrow & Ball No. 291 · School House White — тёплый меловой белый · Anti-Reflex 2 · глубокомат. · кл. 2
- **K10** Farrow & Ball No. 291 · School House White — тёплый меловой белый · МДФ · полуглянц. · кл. 2
- **K11** Atlas Concorde A8UZ · Marvel Travertine · Marvel Travertine
- **K12** Farrow & Ball No. 291 · School House White — тёплый меловой белый · Luja 7 · полуматов. · кл. 1
- **K13** Farrow & Ball No. 291 · School House White — тёплый меловой белый · Luja 7 · матовая · кл. 1
- **K14** NCS S 0502-Y · Белый с лёгкой желтизной · Tikkurila Luja 7 · матовая · кл. 1
- **KM1** инженерная доска · 1167-4250
- **KM2** аналог: керамогранит матовый, тон F497, 600×600×9 мм

дерево (доска, паркет, ламинат) — рисунок досок

керамогранит, плитка, камень — сетка швов по формату

HEX не задан — цвет только по коду и вееру

K — позиция окраски (код + продукт + блеск), KM — позиция материала, тон KM — по описанию артикула, эталон — образец материала; ≈ LRV — расчёт по HEX, справочно

Допущения и предложения на листе

Основа листа: размеры сняты со скана обмерного плана KV design (см): часть подписей не читается, помещения выровнены по читаемым размерам; контрольный обмер не выполнен (К-1); высота потолка 2650 мм принята по отметкам обмера (Н = 2,50…2,66 м, ригель 2,28 м) — уточнить при обмере (К-2); толщины стен 300 / 120 мм приняты, межквартирная стена и колонны — по скану, не замерены (К-1); разрешённая мощность 15 кВт принята по типовым ТУ; при объединении двух квартир — переоформление ТУ (К-4).

Знак «**» — предложение проектировщика, заказчиком не утверждено (согласовать с заказчиком): записи в реестре нет: плинтус пом. 1–5, 7–10, акцент пом. 3, фартук пом. 5 — артикул изделия не выбран: позиция описана характеристиками («аналог по характеристикам»), артикул выбирается при закупке.

См. лист открытых вопросов (лист 6, записи К-1, К-2, К-4).

Изм.	Кол.уч	Лист	№ док.	Подп.	Дата
Разраб.		Кырлан А.С.			18.10.26
Пров.					
ГИП					
Н. контр.					
Утв.					

ГД-2026-009-АИ

Квартира 103 м²

Общая площадь 100,72* м² · * размеры со скана, не замерены (реестр — л. 6, К-1)

Дизайн-проект интерьера

Стадия	Лист	Листов
РП	43	96

Колерная карта

М б/м

Кырлан Александр Сергеевич

Спецификация отделочных материалов

ПРЕДВАРИТЕЛЬНО · не для производства работ · открыто пунктов: 4 (реестр — л. 6)

Форма 1 по ГОСТ 21.110-2013 · количества — из геометрии проекта, с запасом · часть 1 из 2

Поз.	Наименование и техническая характеристика	Тип, марка, обозначение документа	Код продукции	Поставщик	Ед. изм.	Кол.	Масса 1 ед., кг	Примечание
	Лакокрасочные материалы							
1	Краска интерьерная водно-дисперсионная акриловая для стен, матовая, класс мокрого истирания 1 по EN 13300, база A; цвет Farrow & Ball No. 291 «School House White — тёплый меловой белый», колеровка машинная	Farrow & Ball Modern Emulsion		Farrow & Ball	л	40		поз. К1 колерной карты; пом. 1, 4, 8, 9, 10; S = 141,8 м² × 2 сл. × 0,12 л/м² = 34,0 л, +10 % и 0,5 л на подкраску → ≥ 37,9 л; тара 8 × 5 л
2	Краска интерьерная водно-дисперсионная акриловая для акцентных стен, матовая, класс мокрого истирания 1 по EN 13300, база C; цвет Farrow & Ball No. 289 «Inchyra Blue — тёмный сине-серый», колеровка машинная	Farrow & Ball Modern Emulsion		Farrow & Ball	л	12,5		поз. К2 колерной карты; пом. 1, 8, 10; S = 37,0 м² × 2 сл. × 0,12 л/м² = 8,9 л, +10 % и 0,5 л на подкраску → ≥ 10,3 л; тара 2 × 5 л + 1 × 2,5 л
3	Краска интерьерная водно-дисперсионная акриловая для потолков, глубокоматовая, класс мокрого истирания 2 по EN 13300, база A; цвет NCS S 0502-Y «Белый с лёгкой желтизной», колеровка машинная	Tikkurila Anti-Reflex 2		Tikkurila	л	18,9		поз. К3 колерной карты; пом. 1, 2, 4, 7, 8, 9, 10; S = 67,8 м² × 2 сл. × 0,12 л/м² = 16,3 л, +10 % и 0,5 л на подкраску → ≥ 18,4 л; тара 2 × 9 л + 1 × 0,9 л
4	Краска интерьерная водно-дисперсионная акриловая для стен, матовая, класс мокрого истирания 1 по EN 13300, база A; цвет NCS S 0502-Y «Белый с лёгкой желтизной», колеровка машинная	Tikkurila Harmony		Tikkurila	л	9		поз. К5 колерной карты; пом. 2, 7; S = 29,5 м² × 2 сл. × 0,12 л/м² = 7,1 л, +10 % и 0,5 л на подкраску → ≥ 8,3 л; тара 1 × 9 л
5	Краска интерьерная водно-дисперсионная акриловая для стен, матовая, класс мокрого истирания 2 по EN 13300, база A; цвет Farrow & Ball No. 291 «School House White — тёплый меловой белый», колеровка машинная	Tikkurila Optiva 5 Matt		Tikkurila	л	7,5		поз. К7 колерной карты; пом. 3; S = 24,9 м² × 2 сл. × 0,12 л/м² = 6,0 л, +10 % и 0,5 л на подкраску → ≥ 7,1 л; тара 1 × 5 л + 1 × 2,5 л
6	Краска интерьерная водно-дисперсионная акриловая для акцентных стен, матовая, класс мокрого истирания 2 по EN 13300, база C; цвет Farrow & Ball No. 255 «Tanner's Brown — тёмный шоколад», колеровка машинная	Tikkurila Optiva 5 Matt		Tikkurila	л	7,5		поз. К8 колерной карты; пом. 3; S = 12,3 м² × 3 сл. × 0,12 л/м² = 4,4 л, +10 % и 0,5 л на подкраску → ≥ 5,4 л; тара 1 × 5 л + 1 × 2,5 л
7	Краска интерьерная водно-дисперсионная акриловая для потолков, глубокоматовая, класс мокрого истирания 2 по EN 13300, база A; цвет Farrow & Ball No. 291 «School House White — тёплый меловой белый», колеровка машинная	Tikkurila Anti-Reflex 2		Tikkurila	л	7,5		поз. К9 колерной карты; пом. 3; S = 20,3 м² × 2 сл. × 0,12 л/м² = 4,9 л, +10 % и 0,5 л на подкраску → ≥ 5,9 л; тара 1 × 5 л + 1 × 2,5 л
8	Краска интерьерная водно-дисперсионная акриловая для стен, полуматовая, класс мокрого истирания 1 по EN 13300, база A; цвет Farrow & Ball No. 291 «School House White — тёплый меловой белый», колеровка машинная	Tikkurila Luja 7		Tikkurila	л	7,5		поз. К12 колерной карты; пом. 5; S = 21,9 м² × 2 сл. × 0,12 л/м² = 5,2 л, +10 % и 0,5 л на подкраску → ≥ 6,3 л; тара 1 × 5 л + 1 × 2,5 л
9	Краска интерьерная водно-дисперсионная акриловая для потолков, матовая, класс мокрого истирания 1 по EN 13300, база A; цвет Farrow & Ball No. 291 «School House White — тёплый меловой белый», колеровка машинная	Tikkurila Luja 7		Tikkurila	л	2,5		поз. К13 колерной карты; пом. 5; S = 6,5 м² × 2 сл. × 0,12 л/м² = 1,6 л, +10 % и 0,5 л на подкраску → ≥ 2,2 л; тара 1 × 2,5 л
10	Краска интерьерная водно-дисперсионная акриловая для потолков, матовая, класс мокрого истирания 1 по EN 13300, база A; цвет NCS S 0502-Y «Белый с лёгкой желтизной», колеровка машинная	Tikkurila Luja 7		Tikkurila	л	2,7		поз. К14 колерной карты; пом. 6, 11; S = 6,0 м² × 2 сл. × 0,12 л/м² = 1,4 л, +10 % и 0,5 л на подкраску → ≥ 2,1 л; тара 1 × 2,7 л
11	Краска для МДФ и дерева в цвет Farrow & Ball No. 291 «School House White — тёплый меловой белый» — окраска плинтуса; блеск не ниже блеска стен	марка не задана			л	2,4		поз. К4, К10; пом. 1, 3, 4, 5, 8, 9, 10; L = 92,6 м, S = 8,9 м² × 2 сл. × 0,12 л/м² + 10 %; продукт подобрать в веере Farrow & Ball
12	Краска для МДФ и дерева в цвет NCS S 0502-Y «Белый с лёгкой желтизной» — окраска плинтуса; блеск не ниже блеска стен	марка не задана			л	0,5		поз. К6; пом. 2, 7; L = 10,8 м, S = 1,0 м² × 2 сл. × 0,12 л/м² + 10 %; продукт подобрать в веере NCS
13	Грунтовка акриловая под окраску стен и потолков — из системы производителя краски	по системе краски			м²	369		площадь окраски стен, акцентов и потолков; 1 слой перед окраской; расход — по ТУ грунтовки

Допущения и предложения на листе

Основа листа: размеры сняты со скана обмерного плана KV design (см): часть подписей не читается, помещения выровнены по читаемым размерам; контрольный обмер не выполнен (К-1); высота потолка 2650 мм принята по отметкам обмера (Н = 2,50…2,66 м, ригель 2,28 м) — уточнить при обмере (К-2); толщины стен 300 / 120 мм приняты, межквартирная стена и колонны — по скану, не замерены (К-1); разрешённая мощность 15 кВт принята по типовым ТУ; при объединении двух квартир — переоформление ТУ (К-4).

Знак «**» — предложение проектировщика, заказчиком не утверждено (согласовать с заказчиком): записи в реестре нет: плинтус пом. 1–5, 7–10, акцент пом. 3, фартук пом. 5 — артикул изделия не выбран: позиция описана характеристиками («аналог по характеристикам»), артикул выбирается при закупке.

См. лист открытых вопросов (лист 6, записи К-1, К-2, К-4).

Изм.	Кол.уч	Лист	№ док.	Подп.	Дата
Разраб.		Кырлан А.С.			18.10.26
Пров.					
ГИП					
Н. контр.					
Утв.					

ГД-2026-009-АИ

Квартира 103 м²

Общая площадь 100,72* м² · * размеры со скана, не замерены (реестр — л. 6, К-1)

	Стадия	Лист	Листов
Дизайн-проект интерьера	РП	44	96

Спецификация отделочных материалов

М б/м

Кырлан Александр Сергеевич

Спецификация отделочных материалов

ПРЕДВАРИТЕЛЬНО · не для производства работ · открыто пунктов: 4 (реестр — л. 6)

Форма 1 по ГОСТ 21.110-2013 · количества — из геометрии проекта, с запасом · часть 2 из 2

Поз.	Наименование и техническая характеристика	Тип, марка, обозначение документа	Код продукции	Поставщик	Ед. изм.	Кол.	Масса 1 ед., кг	Примечание
	Плитка и керамогранит							
14	Керамогранит под травертин, 600×600 мм	аналог по характеристикам			м²	9,36		шов 2 мм; Ванная, пол; Ванная мастер, пол; по раскладке 23 шт (S = 6,04 м²), с запасом 26 шт
15	Керамогранит под травертин, 600×1200×9 мм, ректификат, водопоглощение 0,1 %	аналог по характеристикам		Atlas Concorde	м²	54,72		шов 2 мм; Ванная, стены А–Г; Ванная, короб инсталляции; Ванная мастер, стены А–Г; Ванная мастер, короб инсталляции; по раскладке 66 шт (S = 32,12 м²), с запасом 76 шт
16	A8UZ, 600×1200×9 мм, ректификат, водопоглощение 0,1 % (BIa), противоскольжение R10, PEI IV	A8UZ		Atlas Concorde	м²	15,84		шов 2 мм; Прихожая-холл, пол; по раскладке 20 шт (S = 12,91 м²), с запасом 22 шт
17	Керамогранит матовый, тон F497, ректификат, водопоглощение 0,5 % (BIa)	аналог по характеристикам			м²	1,85		5. Кухня, фартук; раскладка не выполнена — S = 1,68 м² + 10 %; клей и затирка — по раскладке
	Напольные покрытия							
18	1167-4250, рабочий слой 4 мм, эмиссия E1, укладка на клей	1167-4250		Coswick	м²	87,5		пом. 1, 2, 3, 5, 7, 8, 9, 10; S = 81,77 м² + 7 % (прямая укладка); к заказу — кратно упаковке
19	Клей для паркета и инженерной доски, эластичный (СМП / полиуретановый)	по рекомендации производителя доски			м²	82		площадь приклейки; расход и шпатель — по ТУ клея
	Погонажные изделия							
20	Плинтус МДФ под покраску 80×16, крепление к стене, окраска в цвет Farrow & Ball No. 291	аналог по характеристикам			м	88		пом. 1, 2, 4, 7, 8, 9, 10; L = 79,3 м (периметр без дверных проёмов) + 10 % на подрезку; в штуках — по длине планки
21	Плинтус МДФ под окраску 80×16 мм, крепление к стене, окраска в цвет Farrow & Ball No. 291	аналог по характеристикам			м	27		пом. 3, 5; L = 24,2 м (периметр без дверных проёмов) + 10 % на подрезку; в штуках — по длине планки
	Смеси и материалы для облицовки							
22	Затирка для швов плитки, класс CG2WA по EN 13888	Mapei Ultracolor Plus 132		Mapei	кг	4		по раскладке (a+b)/(a·b) × шов × t × 1,6 + 10 %; в т. ч. 1,0 кг — позиции раскладки без марки
23	Клей плиточный C2 TE S1 по EN 12004, слой 5 мм	Ceresit CM 17		Ceresit	кг	405		17 меш. по 25 кг; 1,5 кг/м² на 1 мм слоя + 10 %; в т. ч. 108 кг — позиции раскладки без марки
24	Гидроизоляция обмазочная мокрых зон: пол, стены по периметру, зоны замачивания; 2 слоя с армирующей лентой в углах	аналог по характеристикам			м²	21,5		площадь по листу раскладки плитки + 10 %; расход смеси — по ТУ
25	Лента демпферная по периметру пола из плитки	аналог по характеристикам			м	27,1		периметр без дверных проёмов + 10 %

Примечания

1. Количества — из геометрии проекта: площади поверхностей по чистым граням стен до отделки (те же, что в ведомости отделки и колерной карте), плитка, клей и затирка — по раскладке плиточника; в графе «Кол.» — к заказу, с запасом.
2. Краска: расход 0,12 л/м² на слой в 2 слоя, если по ТУ не задан иной; запас 10 % и 0,5 л на подкраску каждого кода. Один код — одна партия, колеровка машинная в колеровочном центре бренда; в заказ — только после утверждения выкраса (колерная карта). Фасовка — по каталогу бренда на дату выпуска; к заказу — не меньше расчётного объёма.
3. «Аналог по характеристикам» — допускается изделие другого производителя с характеристиками не ниже указанных, по согласованию с автором проекта.
4. Графы «Код продукции» и «Масса 1 ед.» не заполнены: коды по классификатору продукции не присвоены, масса единицы до 25 кг (ГОСТ 21.110-2013).
5. Грунтовка и клей для доски указаны площадью обработки; объём — по ТУ выбранного продукта.

Допущения и предложения на листе

Основа листа: размеры сняты со скана обмерного плана KV design (см): часть подписей не читается, помещения выровнены по читаемым размерам; контрольный обмер не выполнен (К-1); высота потолка 2650 мм принята по отметкам обмера (Н = 2,50…2,66 м, ригель 2,28 м) — уточнить при обмере (К-2); толщины стен 300 / 120 мм приняты, межквартирная стена и колонны — по скану, не замерены (К-1); разрешённая мощность 15 кВт принята по типовым ТУ; при объединении двух квартир — переоформление ТУ (К-4).

Знак «**» — предложение проектировщика, заказчиком не утверждено (согласовать с заказчиком): записи в реестре нет: плинтус пом. 1–5, 7–10, акцент пом. 3, фартук пом. 5 — артикул изделия не выбран: позиция описана характеристиками («аналог по характеристикам»), артикул выбирается при закупке.

См. лист открытых вопросов (лист 6, записи К-1, К-2, К-4).

Изм.	Кол.уч	Лист	№ док.	Подп.	Дата
Разраб.		Кырлан А.С.			18.10.26
Пров.					
ГИП					
Н. контр.					
Утв.					

ГД-2026-009-АИ

Квартира 103 м²

Общая площадь 100,72* м² · * размеры со скана, не замерены (реестр — л. 6, К-1)

Дизайн-проект интерьера	Стадия	Лист	Листов
	РП	45	96
Спецификация отделочных материалов М б/м	**Кырлан Александр Сергеевич**		

выпуск 18.10.2026 № 53dc234b8d · стр. 54 из 135

Концепция декора и визуализации

Мид-сенчури · ретро с авторской мебелью · визуализации, палитра, материалы, ключевые предметы

ПРЕДВАРИТЕЛЬНО · не для производства работ · открыто пунктов: 4 (реестр — л. 6)

Визуализация 1. Вид сверху (3D): планировка с мебелью, текстилем и декором

Расстановка — по плану мебели (лист 16); шторы, ковры, картины и растения — по плану текстиля и декора (лист 47).

Визуализация 18. Гостиная-столовая (пом. 3)

шторы Т1, Т2 · ковёр Т3 · картина ДК1 · растение ДК2 · подушки, пледы Т4, Т5, Т6

Визуализация 16. Кухня (пом. 5)

шторы Т14 · растение ДК9

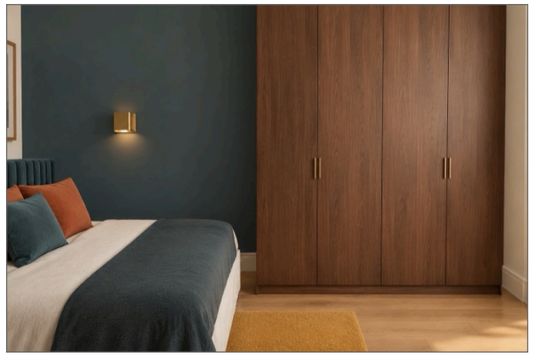

Визуализация 6. Спальня 2 (пом. 8)

шторы Т11, Т13 · ковёр Т15 · картина ДК4 · зеркало ДК6 · подушки, пледы Т16, Т17, Т18

Визуализация 9. Спальня мастер (пом. 10)

шторы Т19, Т20 · ковёр Т21 · картина ДК7 · подушки, пледы Т22, Т23, Т24

Палитра 60/30/10 и цвета текстиля

- Farrow & Ball No. 291 (School House White — тёплый меловой белый), LRV 73 — 60 % база — Т2
- NCS S 1005-Y20R (Светлый кремовый), LRV 77 — 60 % база — Т1, Т4, Т7, Т11, Т14, Т19, Т22
- NCS S 0502-Y (Белый с лёгкой желтизной), LRV 95 — 60 % база — Т8, Т13, Т20
- Farrow & Ball No. 298 (Bancha — оливковый середины века), LRV 14 — 30 % второй цвет — Т3, Т21
- Farrow & Ball No. 289 (Inchyra Blue — тёмный сине-серый), LRV 13 — 30 % второй цвет — Т12, Т18, Т23, Т24
- Farrow & Ball No. 255 (Tanner's Brown — тёмный шоколад), LRV 7 — 30 % второй цвет — Т5, Т6
- NCS S 2050-Y20R (Горчичный), LRV 42 — 10 % акцент — Т9, Т15
- NCS S 3050-Y70R (Терракотовый / жжёный оранжевый), LRV 18 — 10 % акцент — Т10, Т16
- NCS S 5030-B10G (Тил), LRV 12 — 10 % акцент — Т17
- NCS S 5040-B90G (Изумрудный), LRV 8 — 10 % акцент

Материалы и фактуры

Дуб натуральный
пол: пом. 1, 2, 3, 5, 7, 8, 9, 10; рамы ДК3, ДК4, ДК7

Букле
подушки: Т10, Т16

Лён
портьеры, подушки, рулонная: Т1, Т4, Т7, Т11, Т14, Т19, Т22

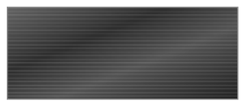

Чёрный матовый металл
рамы ДК5, ДК6 — чёрный

Бархат
подушки: Т5, Т17, Т23

Ключевые предметы

- Диван Г2 2600×900 — гостиная-столовая; подушки и плед Т4, Т5, Т6
- Кровати М1, С1 — над изголовьем картины ДК4, ДК7; текстиль Т16, Т17, Т18, Т22, Т23, Т24
- Ковры Т3, Т9, Т15, Т21 — шерсть, на противоскользящей подложке
- Картины ДК1, ДК3, ДК4, ДК7 — центр на высоте 1450–1650 мм
- Зеркала в рост ДК5, ДК6
- Шторы-волна Т1, Т7, Т11, Т19 (NCS S 1005-Y20R), тюль Т2, Т8, Т13, Т20 (NCS S 0502-Y) — в нишах потолка
- Растение ДК2, растение ДК9

Настроение

Ретро 2026: mid-century 65 % + ар-деко (art-deco.json) 35 %. Стены — School House White No. 291 и кремовый S 1005-Y20R, потолки — белый S 0502-Y; второй план — орех и тик, оливковый Bancha No. 298, сине-серый Inchyra Blue No. 289; акценты — горчица S 2050-Y20R, терракота S 3050-Y70R, тил S 5030-B10G, изумрудный бархат S 5040-B90G; металл — латунь. Мебель — авторские модели середины века (как предложение, модели уточняются с заказчиком). Настроение стиля: оптимизм, функциональность, тёплое дерево, лёгкость, ретро без китча, связь с улицей, графичные акценты. Свет тёплый, 2700–3000 K.

Примечания

1. Визуализации — образ интерьера. Изделия, размеры, высоты подвеса и привязки — по чертежам (план текстиля и декора — лист 47; шторы и карнизы — лист 48; ведомость текстиля — лист 49; ведомость декора и развеска — лист 50); при расхождении действуют чертежи и ведомости.
2. Коды цвета — ориентир подбора по веерам производителей; ткань утверждается по образцу при дневном свете и при свете проекта 2700–3000 K.
3. Мелкий стайлинг на визуализациях (книги, посуда, свечи) в ведомости не входит и поставляется заказчиком по желанию.

Допущения и предложения на листе

Основа листа: размеры сняты со скана обмерного плана KV design (см): часть подписей не читается, помещения выровнены по читаемым размерам; контрольный обмер не выполнен (К-1); высота потолка 2650 мм принята по отметкам обмера (Н = 2,50…2,66 м, ригель 2,28 м) — уточнить при обмере (К-2); толщины стен 300 / 120 мм приняты, межквартирная стена и колонны — по скану, не замерены (К-1); разрешённая мощность 15 кВт принята по типовым ТУ; при объединении двух квартир — переоформление ТУ (К-4).
См. лист открытых вопросов (лист 6, записи К-1, К-2, К-4).

Изм.	Кол.уч	Лист	№ док.	Подп.	Дата
Разраб.		Кырлан А.С.			18.10.26
Пров.					
ГИП					
Н. контр.					
Утв.					

ГД-2026-009-АИ

Квартира 103 м²

Общая площадь 100,72* м² · * размеры со скана, не замерены (реестр — л. 6, К-1)

Дизайн-проект интерьера	Стадия	Лист	Листов
	РП	46	96

Концепция декора и визуализации

М б/м

Кырлан Александр Сергеевич

выпуск 18.10.2026 № 53dc234b8d · стр. 55 из 135

План текстиля и декора

Шторы и карнизы, ковры, картины и зеркала, растения · размеры в мм от чистовых стен и чистого пола · марки — по ведомостям

ПРЕДВАРИТЕЛЬНО · не для производства работ · открыто пунктов: 4 (реестр — л. 6)

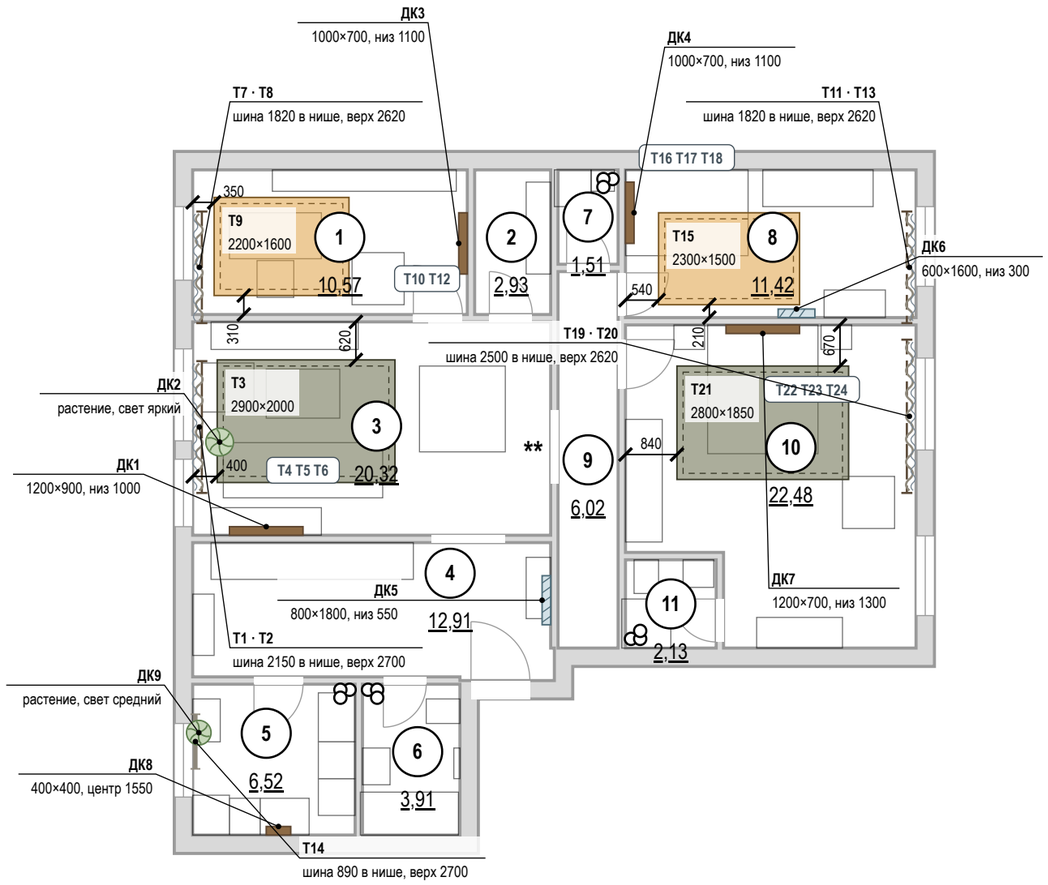

Условные обозначения

- ковёр — габарит в масштабе, цвет изделия
- шина или карниз штор (выше плоскости разреза)
- портьеры (штора-волна)
- тюль (на плане — волнистая линия)
- римская или рулонная штора в проёме
- картина на стене — ширина в масштабе
- зеркало на стене — ширина в масштабе
- растение в кашпо — диаметр в масштабе
- ваза, настольный декор
- подушки, пледы — марки на мебели
- привязка от чистовой стены, мм
- (1) номер помещения, площадь м²
- стены (подложка обмера)
- ** «**» — предложение проектировщика, заказчиком не утверждено

Т1, ДК1 — марки по ведомостям текстиля и декора

Экспликация помещений

лист 12 · на плане — номера в марках

Окна: шина → полотно, мм

Поз.	Шина	Верх шины	Полотно, низ
T7, T8	1820	2620, ниша	2610, низ 10
T1, T2	2150	2700, ниша	2690, низ 10
T14	890	2700, ниша	1900, низ 800
T11, T13	1820	2620, ниша	2610, низ 10
T19, T20	2500	2620, ниша	2610, низ 10

Допущения и предложения на листе

Основа листа: размеры сняты со скана обмерного плана KV design (см): часть подписей не читается, помещения выровнены по читаемым размерам; контрольный обмер не выполнен (К-1); высота потолка 2650 мм принята по отметкам обмера (Н = 2,50…2,66 м, ригель 2,28 м) — уточнить при обмере (К-2); толщины стен 300 / 120 мм приняты, межквартирная стена и колонны — по скану, не замерены (К-1); разрешённая мощность 15 кВт принята по типовым ТУ; при объединении двух квартир — переоформление ТУ (К-4).

Знак «**» — предложение проектировщика, заказчиком не утверждено (согласовать с заказчиком): К-5: дверь пом. 3 (стена Б) — проём в межквартирной стене — объединение квартир, предложение до техзаключения.

См. лист открытых вопросов (лист 6, записи К-1, К-2, К-4, К-5).

Примечания

1. Размеры — в мм. Отступы ковров — от чистовых стен; высоты картин и зеркал — от чистого пола до центра или низа рамы.
2. Шторы — на шинах в нишах потолка (ниша — план потолков, лист 34); закладная под шину — до обшивки ГКЛ. Схемы окон, длины полотен и сборка — лист 48.
3. Картины и зеркала массой более 5 кг — на анкеры по основанию, нагрузка крепежа не меньше двойной массы изделия; на ГКЛ — только по закладной. Декор не перекрывает розетки и выключатели.
4. Ковры на гладком полу — на противоскользящей подложке.
5. Мебель — по плану расстановки мебели (лист 16); ведомость текстиля — лист 49, ведомость декора и схемы развески — лист 50.
6. Номера помещений — по экспликации (лист 12); наименования и площади на этом листе не дублируются.
7. Марки текстиля «Т» и декора «Д» относятся только к листам текстиля и декора; индексы трубопроводов Т1–Т4 — на листах ВК и ОВ.

1000 мм · печать 1:1

Изм.	Кол.уч	Лист	№ док.	Подп.	Дата
Разраб.		Кырлан А.С.			18.10.26
Пров.					
ГИП					
Н. контр.					
Утв.					

ГД-2026-009-АИ

Квартира 103 м²

Общая площадь 100,72* м² · * размеры со скана, не замерены (реестр — л. 6, К-1)

Дизайн-проект интерьера

Стадия	Лист	Листов
РП	47	96

План текстиля и декора

М 1:100

Кырлан Александр Сергеевич

выпуск 18.10.2026 № 53dc234b8d · стр. 56 из 135

08

Декор и текстиль

Кырлан Александр Сергеевич

выпуск 18.10.2026 № 53dc234b8d · стр. 57 из 135

Шторы и карнизы

Схемы окон «шина → полотно» (М 1:100) · отметки от чистого пола помещения · размеры в мм

Окно 1 — Кабинет-библиотека (пом. 1): Т7, Т8 (М 1:100)

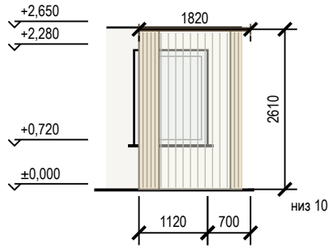

Окно 1 — Гостиная-столовая (пом. 3): Т1, Т2 (М 1:100)

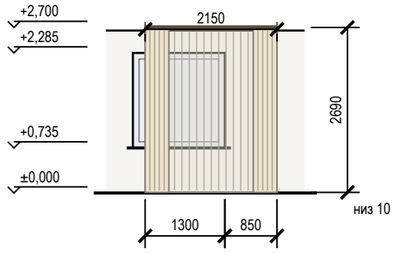

Окно 1 — Кухня (пом. 5): Т14 (М 1:100)

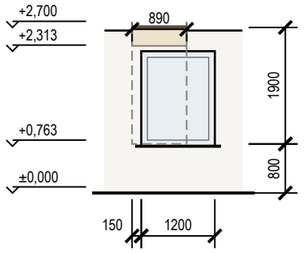

Окно 1 — Спальня 2 (пом. 8): Т11, Т13 (М 1:100)

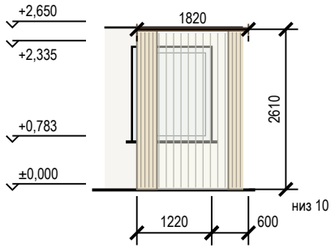

Окно 1 — Спальня мастер (пом. 10): Т19, Т20 (М 1:100)

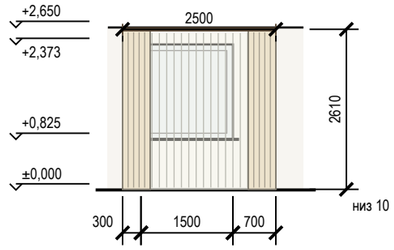

Карта окон: окно → шина → полотно

Поз.	Окно, пом.	Проём Ш×В, подоконник	Верх ниши	Изделие	Шина / карниз: длина, крепление	Верх шины	Полотно: длина, низ	Управление
Т7	1, пом. 1	1200×1560, подок. 720		портьеры	шина, 1820, в нише потолка, вынос 150	+2,620	2610, низ 10 (парит)	вручную
Т8	1, пом. 1	1200×1560, подок. 720		тюль	шина, 1820, в нише потолка, вынос 150	+2,620	2610, низ 10 (парит)	вручную
Т1	1, пом. 3	1500×1550, подок. 735		портьеры	шина, 2150, в нише потолка, вынос 150	+2,700	2690, низ 10 (парит)	вручную
Т2	1, пом. 3	1500×1550, подок. 735		тюль	шина, 2150, в нише потолка, вынос 100	+2,700	2690, низ 10 (парит)	вручную
Т14	1, пом. 5	1200×1550, подок. 763		рулонная штора	шина, 890, в нише потолка, вынос 120	+2,700	1900, низ 800	без шнура
Т11	1, пом. 8	1300×1552, подок. 783		портьеры	шина, 1820, в нише потолка, вынос 150	+2,620	2610, низ 10 (парит)	вручную
Т13	1, пом. 8	1300×1552, подок. 783		тюль	шина, 1820, в нише потолка, вынос 150	+2,620	2610, низ 10 (парит)	вручную
Т19	1, пом. 10	1500×1548, подок. 825		портьеры	шина, 2500, в нише потолка, вынос 150	+2,620	2610, низ 10 (парит)	вручную
Т20	1, пом. 10	1500×1548, подок. 825		тюль	шина, 2500, в нише потолка, вынос 150	+2,620	2610, низ 10 (парит)	вручную

Задания смежникам

Кому	Задание	Пом.
Электрик	выводы под электрокарнизы не требуются (управление вручную)	

Условные обозначения

- портьеры в открытом положении
- римская штора: сложена / опущена
- верх ниши под шторы в потолке
- тюль (на виде окна — прозрачная плашка)
- шина или карниз на отметке верха
- оконный проём

Допущения и предложения на листе

Основа листа: размеры сняты со скана обмерного плана KV design (см): часть подписей не читается, помещения выровнены по читаемым размерам; контрольный обмер не выполнен (К-1); высота потолка 2650 мм принята по отметкам обмера (Н = 2,50…2,66 м, ригель 2,28 м) — уточнить при обмере (К-2); толщины стен 300 / 120 мм приняты, межквартирная стена и колонны — по скану, не замерены (К-1); разрешённая мощность 15 кВт принята по типовым ТУ; при объединении двух квартир — переоформление ТУ (К-4).

Знак «**» — предложение проектировщика, заказчиком не утверждено (согласовать с заказчиком): К-5: дверь пом. 3 (стена Б) — проём в межквартирной стене — объединение квартир, предложение до техзаключения.

См. лист открытых вопросов (лист 6, записи К-1, К-2, К-4, К-5).

Примечания

1. Отметки — от чистого пола помещения; размеры — мм. Длины полотен уточняются замером после чистовой отделки пола и потолка, до раскроя.
2. Карнизы — на анкеры по основанию; на ГКЛ — только по закладной.
3. Полотно портьер «парит» над полом на 10 мм; сборка портьер — 2,0, тюля — 2,5 (ширина полотна — в ведомости текстиля).
4. Шнур римской шторы — с натяжителем, петля низом не ниже 1500 мм от пола (защита детей; EN 13120 — рекомендация).
5. Электрокарнизы не предусмотрены; при замене на электропривод — вывод кабеля в нише у края шины (задание электрику).
6. Марки изделий — по плану текстиля и декора (лист 47) и ведомости текстиля (лист 49).

Изм.	Кол.уч	Лист	№ док.	Подп.	Дата
Разраб.		Кырлан А.С.			18.10.26
Пров.					
ГИП					
Н. контр.					
Утв.					

ГД-2026-009-АИ

Квартира 103 м²

Общая площадь 100,72* м² · * размеры со скана, не замерены (реестр — л. 6, К-1)

Дизайн-проект интерьера

Стадия	Лист	Листов
РП	48	96

Шторы и карнизы

М б/м

Кырлан Александр Сергеевич

выпуск 18.10.2026 № 53dc234b8d · стр. 58 из 135

Ведомость текстиля

Шторы, тюль, римские шторы, ковры, подушки и пледы · размеры в мм · марки — по плану текстиля и декора

Текстиль: шторы, ковры, подушки, пледы

Поз.	Пом.	Изделие	Размер, мм	Ткань, состав, плотность	Сборка, ширина полотна		Цвет (система, код)	Кол.	Примечание
T1	3	Портьеры-волна, два полотна	шина 2150 × полотно 2690	лён 100 %; 280 г/м²	× 2, ширина 4300		NCS S 1005-Y20R (Светлый кремовый)	2	низ 10 (парит); в нише потолка; уход: химчистка; отпаривание на карнизе
T2	3	Тюль-вуаль, одно полотно	шина 2150 × полотно 2690	вуаль; полиэстер 100 %; 60 г/м²	× 2,5, ширина 5375		Farrow & Ball No. 291 (School House White тёплый меловой белый)	1	низ 10 (парит); в нише потолка; уход: стирка 30 °C, вешать влажной
T3	3	Ковёр мягкой группы, абстрактная геометрия середины века	2900×2000	шерсть, плоское плетение; шерсть 100 %			Farrow & Ball No. 298 (Bancha — оливковый середины века)	1	противоскользящая подложка; ворс 8 мм; уход: сухая чистка, пылесос без турбощётки
T4	3	Подушки декоративные на диван	500×500	лён 100 %			NCS S 1005-Y20R (Светлый кремовый)	3	на Г2; уход: съёмный чехол, стирка 30 °C
T5	3	Подушки декоративные на диван, акцент	400×600	хлопковый бархат 100 %			Farrow & Ball No. 255 (Tanner's Brown — тёмный шоколад)	2	на Г2; уход: химчистка
T6	3	Плед на диван	1300×1700	шерсть мериноса 100 %			Farrow & Ball No. 255 (Tanner's Brown — тёмный шоколад)	1	на Г2; уход: ручная стирка 30 °C
T7	1	Портьеры-волна	шина 1820 × полотно 2610	лён с блэкаут-подкладкой; лён 100 %; 320 г/м²	× 2, ширина 3640		NCS S 1005-Y20R (Светлый кремовый)	2	низ 10 (парит); в нише потолка
T8	1	Тюль	шина 1820 × полотно 2610	вуаль; полиэстер 100 %	× 2,5, ширина 4550		NCS S 0502-Y (Белый с лёгкой желтизной)	1	низ 10 (парит); в нише потолка
T9	1	Ковёр под рабочей зоной, геометрия середины века	2200×1600	шерсть, плоское плетение; шерсть 100 %			NCS S 2050-Y20R (Горчичный)	1	противоскользящая подложка; ворс 8 мм
T10	1	Подушки декоративные на кровать	500×500	букле (шерсть 60 %, полиэстер 40 %)			NCS S 3050-Y70R (Терракотовый / жжёный оранжевый)	3	на Б4
T11	8	Портьеры-волна	шина 1820 × полотно 2610	лён с блэкаут-подкладкой; лён 100 %; 320 г/м²	× 2, ширина 3640		NCS S 1005-Y20R (Светлый кремовый)	2	низ 10 (парит); в нише потолка
T12	1	Плед на кровать	1300×1700	шерсть мериноса 100 %			Farrow & Ball No. 289 (Inchyra Blue — тёмный сине-серый)	1	на Б4
T13	8	Тюль	шина 1820 × полотно 2610	вуаль; полиэстер 100 %	× 2,5, ширина 4550		NCS S 0502-Y (Белый с лёгкой желтизной)	1	низ 10 (парит); в нише потолка
T14	5	Рулонная штора кассетная, ткань димаут	шина 890 × полотно 1900	ткань димаут с грязеотталкивающей пропиткой; полиэстер 100 %			NCS S 1005-Y20R (Светлый кремовый)	1	низ 800; в нише потолка; шнур: петля —, cordless; уход: протирка влажной губкой
T15	8	Ковёр под кроватью	2300×1500	шерсть, плоское плетение; шерсть 100 %			NCS S 2050-Y20R (Горчичный)	1	противоскользящая подложка; ворс 8 мм
T16	8	Подушки декоративные на кровать	500×500	букле (шерсть 60 %, полиэстер 40 %)			NCS S 3050-Y70R (Терракотовый / жжёный оранжевый)	3	на С1
T17	8	Подушки на кровать, акцент	400×600	хлопковый бархат 100 %			NCS S 5030-B10G (Тил)	2	на С1
T18	8	Плед на кровать	1300×1700	шерсть мериноса 100 %			Farrow & Ball No. 289 (Inchyra Blue — тёмный сине-серый)	1	на С1
T19	10	Портьеры-волна	шина 2500 × полотно 2610	лён с блэкаут-подкладкой; лён 100 %; 320 г/м²	× 2, ширина 5000		NCS S 1005-Y20R (Светлый кремовый)	2	низ 10 (парит); в нише потолка
T20	10	Тюль	шина 2500 × полотно 2610	вуаль; полиэстер 100 %	× 2,5, ширина 6250		NCS S 0502-Y (Белый с лёгкой желтизной)	1	низ 10 (парит); в нише потолка
T21	10	Ковёр под кроватью	2800×1850	шерсть, ручное ткачество; шерсть 80 %, хлопок 20 %			Farrow & Ball No. 298 (Bancha — оливковый середины века)	1	противоскользящая подложка; ворс 10 мм
T22	10	Подушки декоративные на кровать	500×500	лён 100 %			NCS S 1005-Y20R (Светлый кремовый)	3	на М1
T23	10	Подушки на кровать, акцент	400×600	хлопковый бархат 100 %			Farrow & Ball No. 289 (Inchyra Blue — тёмный сине-серый)	2	на М1
T24	10	Плед на кровать	1300×1700	шерсть мериноса 100 %			Farrow & Ball No. 289 (Inchyra Blue — тёмный сине-серый)	1	на М1

образец цвета — по HEX производителя краски, справочно

Итого: шторы и тюль — 13 шт.; ковры и дорожки — 4 шт.; подушки, пледы, покрывала — 22 шт.

Примечания

1. Коды цвета — ориентир подбора по веерам производителей красок; ткань утверждается по образцу при дневном свете и при свете проекта 2700–3000 K.
2. Размеры полотен — по замеру после чистовой отделки пола и потолка; ширина полотна указана с учётом сборки, без припусков на швы. Схемы окон и отметки шин лист 48.
3. Портьеры и тюль — на тесьме «волна» по системе шины; блэкаут — подкладкой. Ковры — на противоскользящей подложке.
4. Замена изделия — аналогом по характеристикам (состав, плотность, размер, цвет по образцу) с согласованием автора проекта.
5. Места изделий — план текстиля и декора (лист 47); подушки и пледы — по марке мебели.

Допущения и предложения на листе

Основа листа: размеры сняты со скана обмерного плана KV design (см): часть подписей не читается, помещения выровнены по читаемым размерам; контрольный обмер не выполнен (К-1); высота потолка 2650 мм принята по отметкам обмера (Н = 2,50…2,66 м, ригель 2,28 м) — уточнить при обмере (К-2); толщины стен 300 / 120 мм приняты, межквартирная стена и колонны — по скану, не замерены (К-1); разрешённая мощность 15 кВт принята по типовым ТУ; при объединении двух квартир — переоформление ТУ (К-4).
См. лист открытых вопросов (лист 6, записи К-1, К-2, К-4).

Изм.	Кол.уч	Лист	№ док.	Подп.	Дата
Разраб.		Кырлан А.С.			18.10.26
Пров.					
ГИП					
Н. контр.					
Утв.					

ГД-2026-009-АИ

Квартира 103 м²

Общая площадь 100,72* м² · * размеры со скана, не замерены (реестр — л. 6, К-1)

Дизайн-проект интерьера

Стадия	Лист	Листов
РП	49	96

Ведомость текстиля

М б/м

Кырлан Александр Сергеевич

выпуск 18.10.2026 № 53dc234b8d · стр. 59 из 135

Ведомость декора. Схемы развески

Картины, зеркала, растения, настольный декор · схемы развески (М 1:50) · высоты — мм от чистого пола

ПРЕДВАРИТЕЛЬНО · не для производства работ · открыто пунктов: 4 (реестр — л. 6)

Декор: картины, зеркала, растения, предметы

картина · зеркало · мебель под изделием

Поз.	Пом.	Предмет	Размер, мм	Место: стена, высота от пола, мм	Масса, кг	Крепёж и основание	Свет места, отделка	Кол.
ДК1	3	Картина над буфетом	1200×900	стена В, привязка 600; низ 1000, центр 1450; над Г6	6	планка на дюбелях, 4 точки; основание: перегородка 120 мм; нагрузка 20 кг		1
ДК2	3	Фикус лировидный в кашпо Ø400	450×450	напольное			свет яркий рассеянный	1
ДК3	1	Картина над креслом	1000×700	стена Б, привязка 700; низ 1100, центр 1450; над Б4	4	подвес по основанию, 2 точки	рама — дуб	1
ДК4	8	Картина над кроватью	1000×700	стена Г, привязка 200; низ 1100, центр 1450; над С1	4	подвес по основанию, 2 точки	рама — дуб	1
ДК5	4	Зеркало	800×1800	стена Б, привязка 540; низ 550, центр 1450	18	анкер, 4 шт.; основание: перегородка — определить обмером до монтажа; нагрузка 40 кг	рама — чёрный матовый металл	1
ДК6	8	Зеркало в рост в тонкой чёрной раме	600×1600	стена В, привязка 2490; низ 300, центр 1100	12	анкер для пустотелых оснований, 4 шт.; основание: перегородка — определить обмером до монтажа; нагрузка 30 кг	рама — чёрный матовый металл	1
ДК7	10	Картина над кроватью	1200×700	стена А, привязка 1640; низ 1300, центр 1650; над М1	4	подвес по основанию, 2 точки	рама — дуб	1
ДК8	5	Часы настенные Ø400	400×400	стена В, привязка 1200; центр 1550	2	дюбель с крюком, 1 точка; основание: перегородка 120 мм; нагрузка 10 кг		1
ДК9	5	Хлорофитум хохлатый на подоконнике (отм. +0,800)	300×200	напольное			свет средний	1

ДК1 — Гостиная-столовая (пом. 3), стена В (М 1:50)

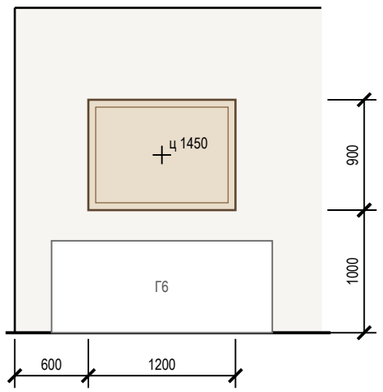

ДК3 — Кабинет-библиотека (пом. 1), стена Б (М 1:50)

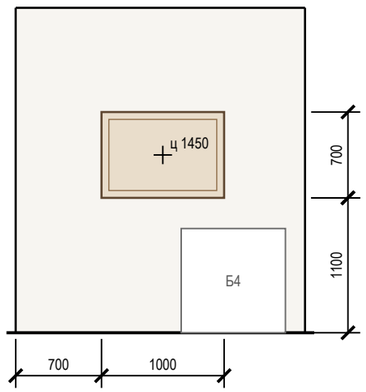

ДК4 — Спальня 2 (пом. 8), стена Г (М 1:50)

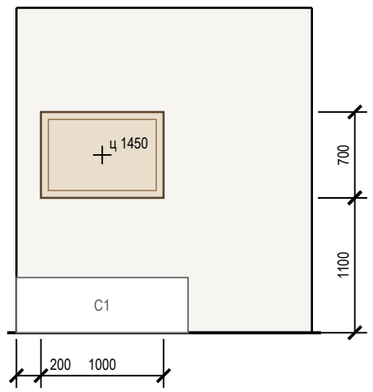

ДК5 — Прихожая-холл (пом. 4), стена Б (М 1:50)

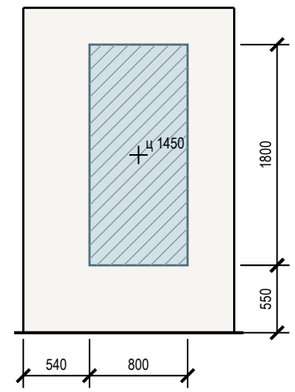

ДК6 — Спальня 2 (пом. 8), стена В (М 1:50)

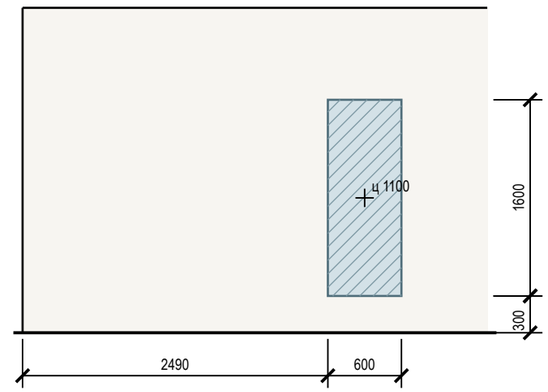

ДК7 — Спальня мастер (пом. 10), стена А (М 1:50)

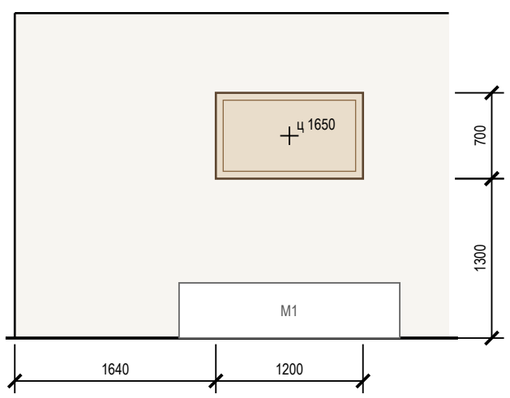

ДК8 — Кухня (пом. 5), стена В (М 1:50)

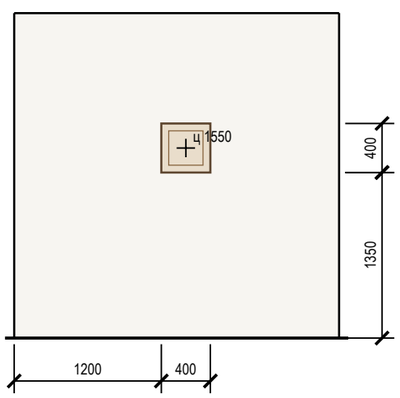

Допущения и предложения на листе

Основа листа: размеры сняты со скана обмерного плана KV design (см): часть подписей не читается, помещения выровнены по читаемым размерам; контрольный обмер не выполнен (К-1); высота потолка 2650 мм принята по отметкам обмера (Н = 2,50…2,66 м, ригель 2,28 м) — уточнить при обмере (К-2); толщины стен 300 / 120 мм приняты, межквартирная стена и колонны — по скану, не замерены (К-1); разрешённая мощность 15 кВт принята по типовым ТУ; при объединении двух квартир — переоформление ТУ (К-4).

См. лист открытых вопросов (лист 6, записи К-1, К-2, К-4).

Примечания

1. Высоты — от чистого пола помещения до низа изделия, «ц» — до центра; привязки — от чистовой грани угла стены, мм.
2. Над мебелью низ изделия — на 150–250 мм выше спинки или изголовья; без мебели центр — на 1450–1600 мм от пола.
3. Изделия до 5 кг — на два подвеса по основанию; тяжелее — на анкеры с нагрузкой не меньше двойной массы; на ГКЛ — только по закладной или анкеру для пустотелых оснований.
4. Зеркала в рост — с креплением от опрокидывания; в санузлах — влагостойкие, на клей для зеркал и нейтральный силикон.
5. Места изделий — план текстиля и декора (лист 47).

Изм.	Кол.уч	Лист	№ док.	Подп.	Дата
Разраб.		Кырлан А.С.			18.10.26
Пров.					
ГИП					
Н. контр.					
Утв.					

ГД-2026-009-АИ

Квартира 103 м²

Общая площадь 100,72* м² · * размеры со скана, не замерены (реестр — л. 6, К-1)

Дизайн-проект интерьера

Стадия	Лист	Листов
РП	50	96

Ведомость декора. Схемы развески

М б/м

Кырлан Александр Сергеевич

выпуск 18.10.2026 № 53dc234b8d · стр. 60 из 135

Встроенная мебель. Схема расположения

встроенная и корпусная мебель на заказ, кухонный гарнитур · размеры в мм · марки — по ведомости изделий

ПРЕДВАРИТЕЛЬНО · не для производства работ · открыто пунктов: 4 (реестр — л. 6)

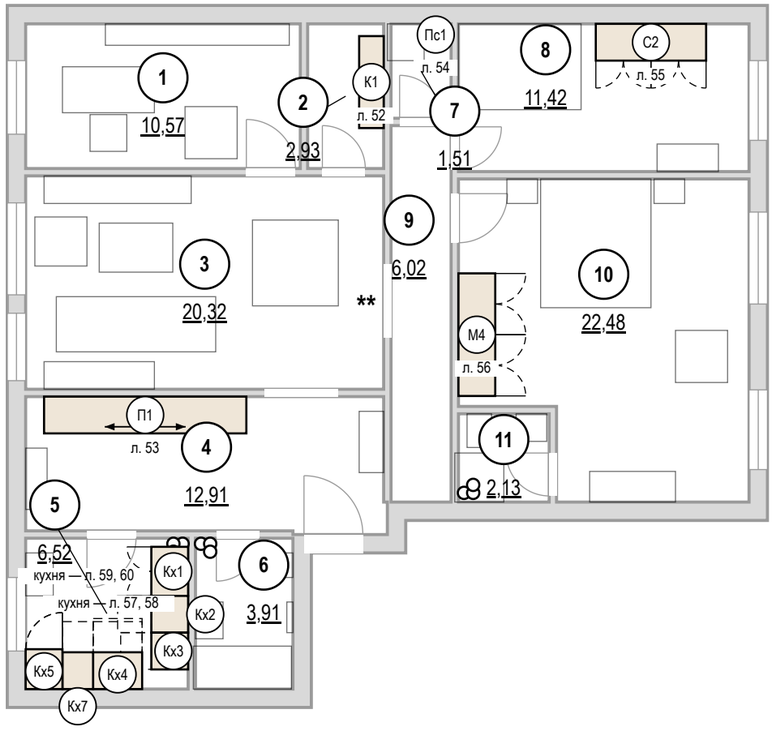

Ведомость изделий

Марка	Наименование	Пом.	Ш×Г×В, мм	Лист
К1	Система хранения	2	1500×400×2400	52
П1	Шкаф-купе	4	3300×600×2600	53
Пс1	Система хранения	7	380×350×2000	54
С2	Шкаф распашной	8	1800×600×2400	55
М4	Шкаф распашной	10	2000×600×2400	56
Кх1	Модуль нижний: мойка	5	800×600×900	57
Кх2	Модуль нижний: ПММ	5	600×600×900	57
Кх3	Модуль нижний: ящики	5	600×600×900	57
Кх4	Модуль нижний: духовой шкаф, варочная	5	800×600×900	59
Кх7	Модуль нижний: ящики	5	500×600×900	59
Кх5	Пенал: холодильник встр.	5	600×650×2100	59

Условные обозначения

- изделие мебельщика: корпус на полу
- навесной модуль (невидимый контур)
- открывание распашного фасада
- зона выдвижения ящика, двери техники
- дверь купе, стрелка — направление движения
- (П5) марка изделия, под ней — лист изделия
- ** «**» — предложение проектировщика, заказчиком не утверждено

Допущения и предложения на листе

Основа листа: размеры сняты со скана обмерного плана KV design (см): часть подписей не читается, помещения выровнены по читаемым размерам; контрольный обмер не выполнен (К-1); высота потолка 2650 мм принята по отметкам обмера (Н = 2,50…2,66 м, ригель 2,28 м) — уточнить при обмере (К-2); толщины стен 300 / 120 мм приняты, межквартирная стена и колонны — по скану, не замерены (К-1); разрешённая мощность 15 кВт принята по типовым ТУ; при объединении двух квартир — переоформление ТУ (К-4).

Знак «**» — предложение проектировщика, заказчиком не утверждено (согласовать с заказчиком): К-5: дверь пом. 3 (стена Б) — проём в межквартирной стене — объединение квартир, предложение до техзаключения.

См. лист открытых вопросов (лист 6, записи К-1, К-2, К-4, К-5).

Примечания

1. Изделия — по чистовым размерам помещений; перед раскроем — контрольный замер цеха после чистовой отделки стен, пола и потолка.
2. Открывание фасадов и выдвижение ящиков показано в открытом положении: зоны не пересекают двери, радиаторы, выключатели и проходы.
3. Стояки и счётчики за мебелью — с сервисным люком; газовые трубы мебелью не зашиваются.
4. Покупная мебель — по плану расстановки мебели и спецификации дизайнера; здесь — подложкой.

1000 мм · печать 1:1

Изм.	Кол.уч	Лист	№ док.	Подп.	Дата
Разраб.		Кырлан А.С.			18.10.26
Пров.					
ГИП					
Н. контр.					
Утв.					

ГД-2026-009-АИ

Квартира 103 м²

Общая площадь 100,72* м² · * размеры со скана, не замерены (реестр — л. 6, К-1)

Дизайн-проект интерьера

Стадия	Лист	Листов
РП	51	96

Встроенная мебель. Схема расположения

М 1:100

Кырлан Александр Сергеевич

выпуск 18.10.2026 № 53dc2348d8d · стр. 61 из 135

Система хранения К1

Кладовая (пом. 2) · вид из помещения · размеры в мм, отметки в м

ПРЕДВАРИТЕЛЬНО · не для производства работ · открыто пунктов: 4 (реестр — л. 6)

Общий вид

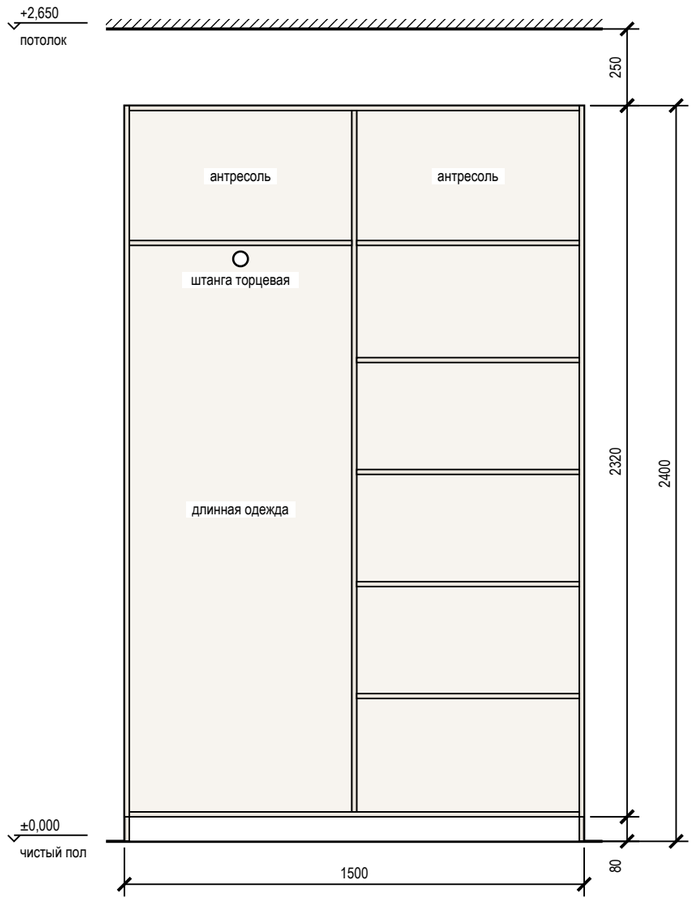

Наполнение, размеры в свету

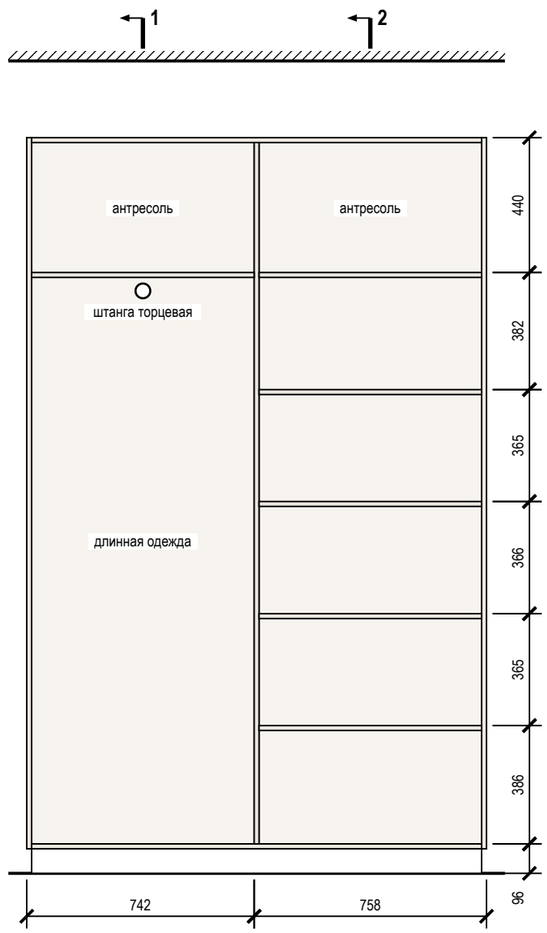

Разрез 1-1

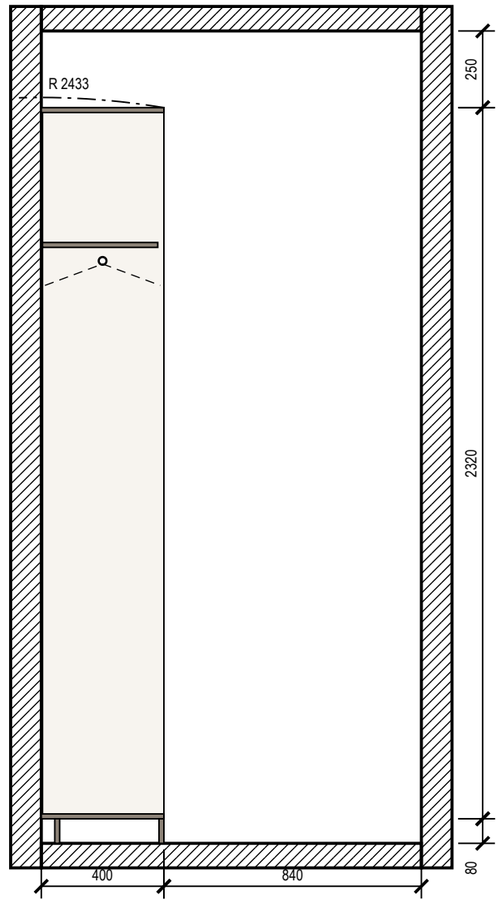

Разрез 2-2

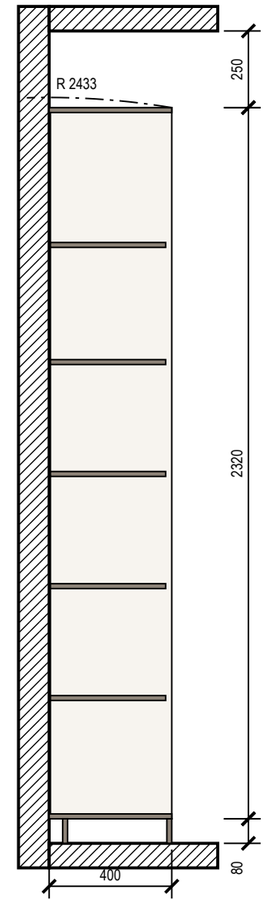

Примечания

1. Размеры — в мм по чистовой отделке; изделие 1500×400×2400 (Ш×Г×В). Перед раскроем — контрольный замер цеха после чистовой отделки стен, пола и потолка.
2. Корпус — ЛДСП 16 мм, задняя стенка ХДФ 4 мм в паз, цоколь 80 мм на регулируемых опорах; открытая система без фасадов, ящики с фасадами.
3. Кромка: скрытые торцы 0,4 мм, видимые 2 мм (ПВХ/АБС).
4. Номинальные зазоры: между фасадами ящиков 3 мм, фасад ящика — стойка 2 мм.
5. Ящики — направляющие полного выдвижения NL 350 (внутренняя глубина 396 мм ≥ NL + 3); присадка по 32-й системе — выполняет цех.
6. Зазор до потолка 250 мм.
7. Подъём корпуса: диагональ боковины √(2400² + 400²) = 2433 мм < 2650 мм до потолка — корпус собирается лёжа и поднимается поворотом.
8. Крепление к стене от опрокидывания — уголки 2 шт. к несущему основанию (монтажная схема шкафов).
9. Проход перед изделием 840 мм показан на разрезе 1-1.

Условные обозначения

- корпус и полки ЛДСП (вид на стену)
- задняя стенка ХДФ
- деталь в разрезе
- штанга для плечиков (на разрезе — плечики 450 мм)
- траектория угла корпуса при подъёме в проектное положение

Допущения и предложения на листе

Основа листа: размеры сняты со скана обмерного плана KV design (см): часть подписей не читается, помещения выровнены по читаемым размерам; контрольный обмер не выполнен (К-1); высота потолка 2650 мм принята по отметкам обмера (Н = 2,50…2,66 м, ригель 2,28 м) — уточнить при обмере (К-2); толщины стен 300 / 120 мм приняты, межквартирная стена и колонны — по скану, не замерены (К-1); разрешённая мощность 15 кВт принята по типовым ТУ; при объединении двух квартир — переоформление ТУ (К-4).
См. лист открытых вопросов (лист 6, записи К-1, К-2, К-4).

1000 мм · печать 1:1

Изм.	Кол.уч	Лист	№ док.	Подп.	Дата
Разраб.		Кырлан А.С.			18.10.26
Пров.					
ГИП					
Н. контр.					
Утв.					

ГД-2026-009-АИ

Квартира 103 м²

Общая площадь 100,72* м² · * размеры со скана, не замерены (реестр — л. 6, К-1)

Дизайн-проект интерьера

Стадия	Лист	Листов
РП	52	96

Система хранения К1

М 1:20

Кырлан Александр Сергеевич

выпуск 18.10.2026 № 53dc234b8d · стр. 62 из 135

Шкаф-купе П1

Прихожая-холл (пом. 4) · вид из помещения · размеры в мм, отметки в м

ПРЕДВАРИТЕЛЬНО · не для производства работ · открыто пунктов: 4 (реестр — л. 6)

Вид с фасадами

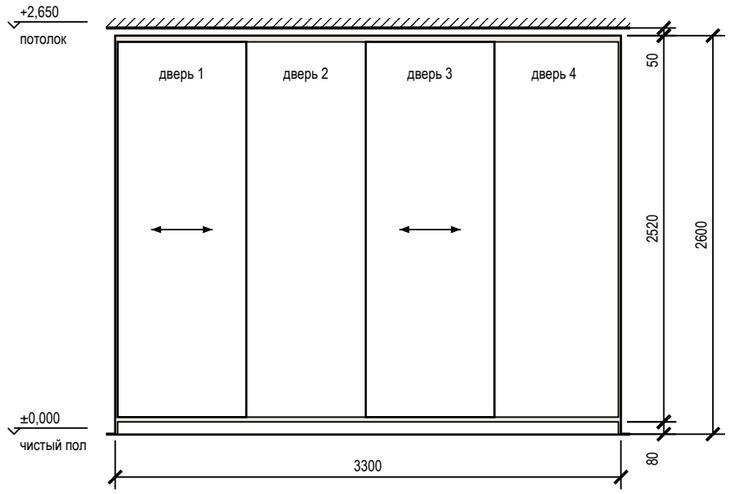

Вид без фасадов

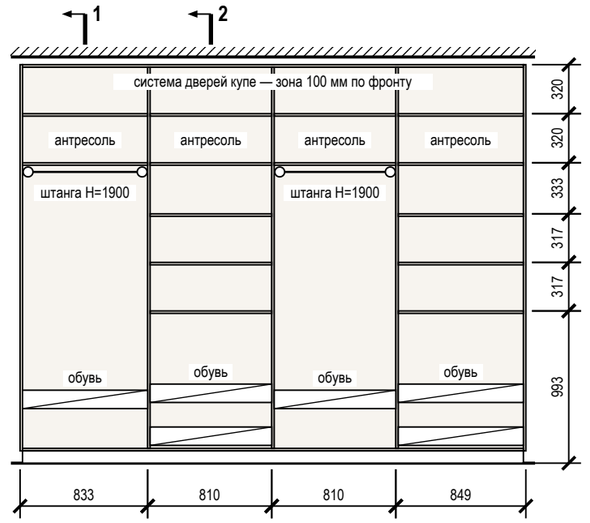

Разрез 1-1

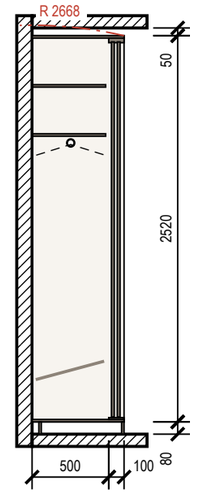

Разрез 2-2

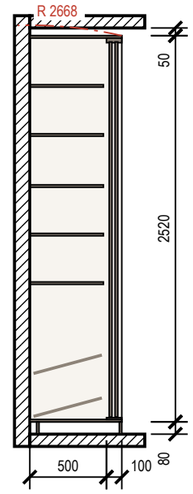

Примечания

1. Размеры — в мм по чистовой отделке; изделие 3300×600×2600 (Ш×Г×В). Перед раскроем — контрольный замер цеха после чистовой отделки стен, пола и потолка.
2. Корпус — ЛДСП 16 мм, задняя стенка ХДФ 4 мм в паз, цоколь 80 мм на регулируемых опорах; двери купе — ЛДСП 10 мм в алюминиевом профиле, нахлёст 30 мм, ширина двери 840 мм, высота — проём минус 40 мм; цвет — по колерной карте.
3. Кромка: скрытые торцы 0,4 мм, видимые 2 мм (ПВХ/АБС).
4. Номинальные зазоры: дверь купе — боковина 3 мм, фасад ящика — стойка 2 мм; ящики внутри купе — с накладкой 30 мм на стойке со стороны нахлёста дверей.
5. Ящики — направляющие полного выдвижения NL 450 (внутренняя глубина 496 мм ≥ NL + 3); присадка по 32-й системе — выполняет цех.
6. Зазор до потолка 50 мм — закрыть планкой в цвет корпуса при монтаже.
7. Подъём корпуса (траектория на виде — красная: корпус не проходит под потолком): диагональ боковины $\sqrt{(2600^2 + 600^2)} = 2668$ мм > 2650 мм до потолка — поднять собранный корпус нельзя: высота корпуса не более 2570 мм, остальное — компенсатор, либо сборка стоя на месте.
8. Крепление к стене от опрокидывания — уголки 2 шт. к несущему основанию (монтажная схема шкафов).

Условные обозначения

- дверь купе, стрелка — направление движения
- корпус и полки ЛДСП (вид на стену)
- задняя стенка ХДФ
- деталь в разрезе
- штанга для плечиков (на разрезе — плечики 450 мм)
- траектория угла корпуса при подъёме в проектное положение

Допущения и предложения на листе

Основа листа: размеры сняты со скана обмерного плана KV design (см): часть подписей не читается, помещения выровнены по читаемым размерам; контрольный обмер не выполнен (К-1); высота потолка 2650 мм принята по отметкам обмера (Н = 2,50…2,66 м, ригель 2,28 м) — уточнить при обмере (К-2); толщины стен 300 / 120 мм приняты, межквартирная стена и колонны — по скану, не замерены (К-1); разрешённая мощность 15 кВт принята по типовым ТУ; при объединении двух квартир — переоформление ТУ (К-4).
См. лист открытых вопросов (лист 6, записи К-1, К-2, К-4).

1000 мм · печать 1:1

Изм.	Кол.уч	Лист	№ док.	Подп.	Дата
Разраб.		Кырлан А.С.			18.10.26
Пров.					
ГИП					
Н. контр.					
Утв.					

ГД-2026-009-АИ

Квартира 103 м²

Общая площадь 100,72* м² · * размеры со скана, не замерены (реестр — л. 6, К-1)

Дизайн-проект интерьера

Стадия	Лист	Листов
РП	53	96

Шкаф-купе П1

М 1:40

Кырлан Александр Сергеевич

выпуск 18.10.2026 № 53dc2340b8d · стр. 63 из 135

Система хранения Пс1

Постирочная (пом. 7) · вид из помещения · размеры в мм, отметки в м

ПРЕДВАРИТЕЛЬНО · не для производства работ · открыто пунктов: 4 (реестр — л. 6)

Общий вид

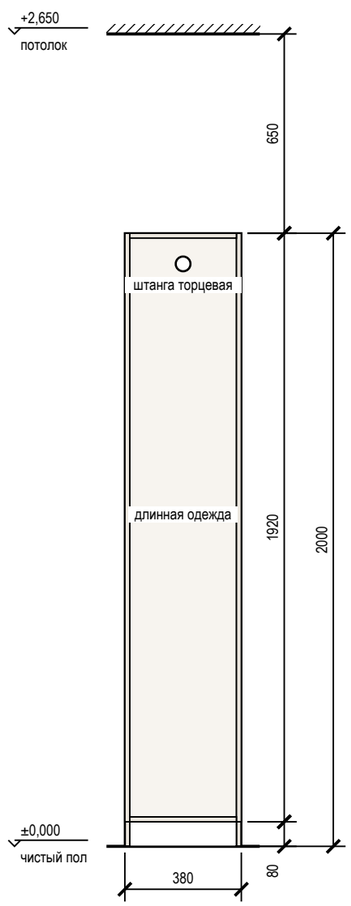

Наполнение, размеры в свету

Разрез 1-1

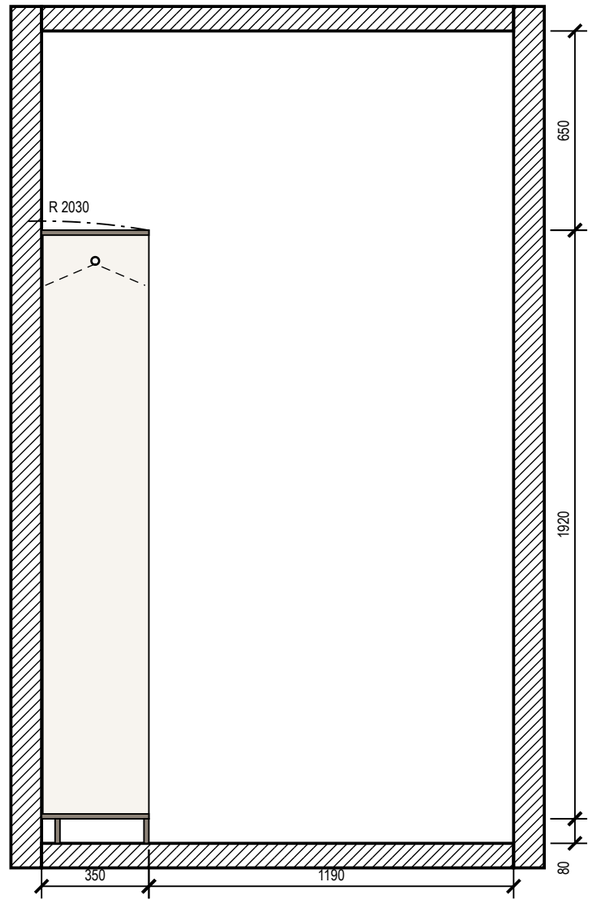

Примечания

1. Размеры — в мм по чистовой отделке; изделие 380×350×2000 (Ш×Г×В). Перед раскроем — контрольный замер цеха после чистовой отделки стен, пола и потолка.
2. Корпус — ЛДСП 16 мм, задняя стенка ХДФ 4 мм в паз, цоколь 80 мм на регулируемых опорах; открытая система без фасадов, ящики с фасадами.
3. Кромка: скрытые торцы 0,4 мм, видимые 2 мм (ПВХ/АБС).
4. Номинальные зазоры: между фасадами ящиков 3 мм, фасад ящика — стойка 2 мм.
5. Ящики — направляющие полного выдвижения NL 300 (внутренняя глубина 346 мм ≥ NL + 3); присадка по 32-й системе — выполняет цех.
6. Зазор до потолка 650 мм.
7. Подъём корпуса: диагональ боковины $\sqrt{(2000^2 + 350^2)} = 2030$ мм < 2650 мм до потолка — корпус собирается лёжа и поднимается поворотом.
8. Крепление к стене от опрокидывания — уголки 2 шт. к несущему основанию (монтажная схема шкафов).
9. Проход перед изделием 1190 мм показан на разрезе 1-1.

Условные обозначения

- корпус и полки ЛДСП (вид на стену)
- задняя стенка ХДФ
- деталь в разрезе
- штанга для плечиков (на разрезе — плечики 450 мм)
- траектория угла корпуса при подъёме в проектное положение

Допущения и предложения на листе

Основа листа: размеры сняты со скана обмерного плана KV design (см): часть подписей не читается, помещения выровнены по читаемым размерам; контрольный обмер не выполнен (К-1); высота потолка 2650 мм принята по отметкам обмера (Н = 2,50…2,66 м, ригель 2,28 м) — уточнить при обмере (К-2); толщины стен 300 / 120 мм приняты, межквартирная стена и колонны — по скану, не замерены (К-1); разрешённая мощность 15 кВт принята по типовым ТУ; при объединении двух квартир — переоформление ТУ (К-4).
См. лист открытых вопросов (лист 6, записи К-1, К-2, К-4).

1000 мм · печать 1:1

Изм.	Кол.уч	Лист	№ док.	Подп.	Дата
Разраб.		Кырлан А.С.			18.10.26
Пров.					
ГИП					
Н. контр.					
Утв.					

ГД-2026-009-АИ

Квартира 103 м²

Общая площадь 100,72* м² · * размеры со скана, не замерены (реестр — л. 6, К-1)

Дизайн-проект интерьера

Стадия	Лист	Листов
РП	54	96

Система хранения Пс1

М 1:20

Кырлан Александр Сергеевич

выпуск 18.10.2026 № 53dc234b8d · стр. 64 из 135

Шкаф распашной С2

Спальня 2 (пом. 8) · вид из помещения · размеры в мм, отметки в м

ПРЕДВАРИТЕЛЬНО · не для производства работ · открыто пунктов: 4 (реестр — л. 6)

Вид с фасадами

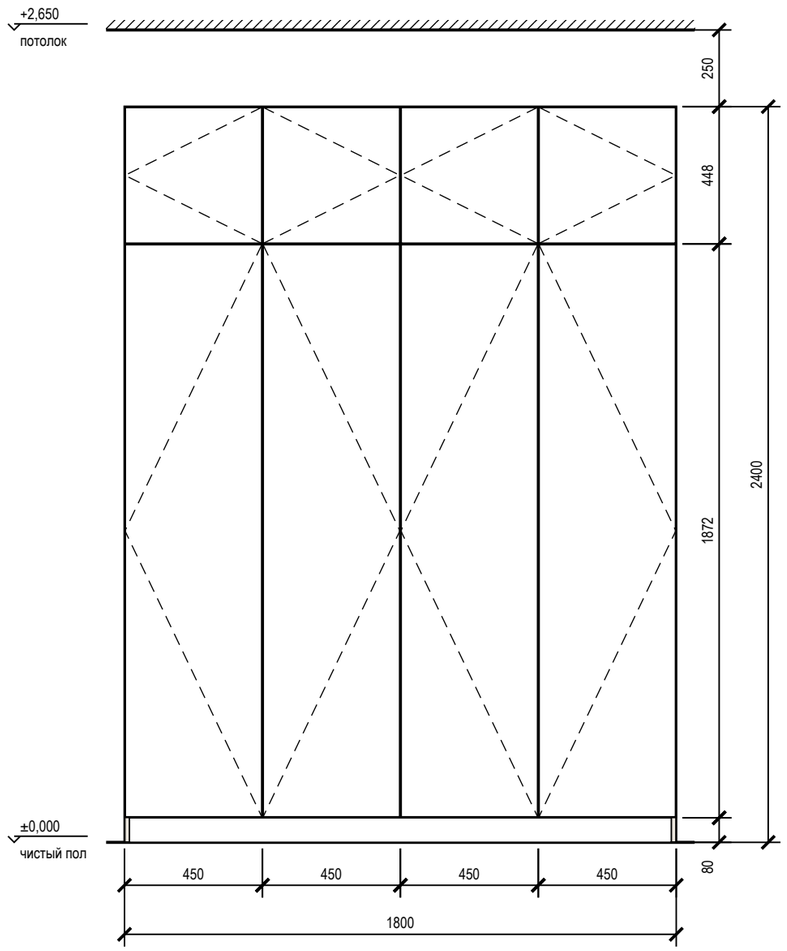

Вид без фасадов

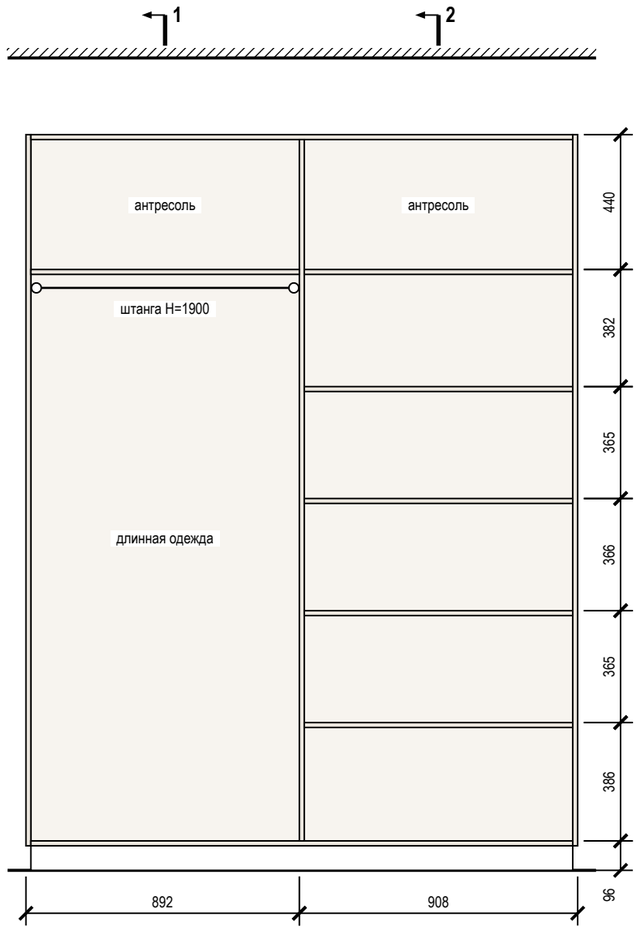

Разрез 1-1

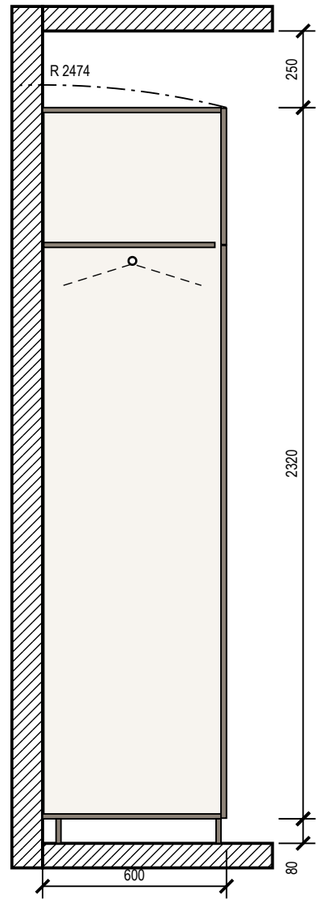

Разрез 2-2

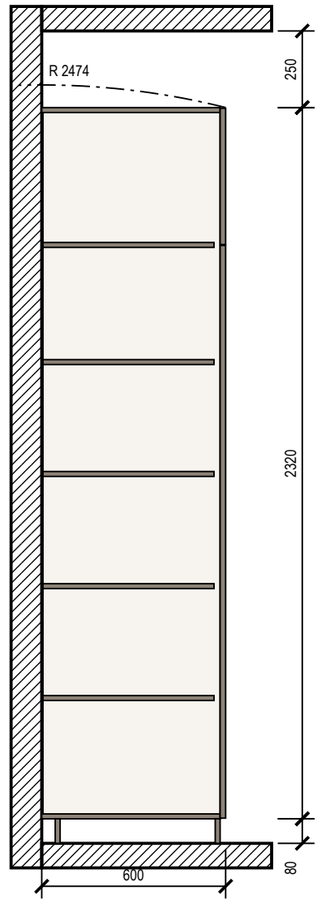

Примечания

1. Размеры — в мм по чистовой отделке; изделие 1800×600×2400 (Ш×Г×В). Перед раскроем — контрольный замер цеха после чистовой отделки стен, пола и потолка.
2. Корпус — ЛДСП 16 мм, задняя стенка ХДФ 4 мм в паз, цоколь 80 мм на регулируемых опорах; фасады — МДФ, эмаль матовая 18 мм накладные, цвет — по колерной карте; петли с доводчиком: фасад 1869 мм — 4 петли, фасад 445 мм — 2 петли.
3. Кромка: скрытые торцы 0,4 мм, видимые 2 мм (ПВХ/АБС).
4. Номинальные зазоры: между фасадами 3 мм, фасад — стена и фасад — потолок не менее 3 мм, фасад ящика — стойка 2 мм.
5. Ящики — направляющие полного выдвижения NL 550 (внутренняя глубина 578 мм ≥ NL + 3); присадка по 32-й системе — выполняет цех.
6. Зазор до потолка 250 мм.
7. Подъём корпуса: диагональ боковины $\sqrt{(2400^2 + 600^2)} = 2474$ мм < 2650 мм до потолка — корпус собирается лёжа и поднимается поворотом.
8. Крепление к стене от опрокидывания — уголки 2 шт. к несущему основанию (монтажная схема шкафов).

Условные обозначения

- фасад распашной: линии сходятся к стороне петель
- корпус и полки ЛДСП (вид на стену)
- задняя стенка ХДФ
- деталь в разрезе
- штанга для плечиков (на разрезе — плечики 450 мм)
- траектория угла корпуса при подъёме в проектное положение

Допущения и предложения на листе

Основа листа: размеры сняты со скана обмерного плана KV design (см): часть подписей не читается, помещения выровнены по читаемым размерам; контрольный обмер не выполнен (К-1); высота потолка 2650 мм принята по отметкам обмера (Н = 2,50…2,66 м, ригель 2,28 м) — уточнить при обмере (К-2); толщины стен 300 / 120 мм приняты, межквартирная стена и колонны — по скану, не замерены (К-1); разрешённая мощность 15 кВт принята по типовым ТУ; при объединении двух квартир — переоформление ТУ (К-4).
См. лист открытых вопросов (лист 6, записи К-1, К-2, К-4).

1000 мм · печать 1:1

Изм.	Кол.уч	Лист	№ док.	Подп.	Дата
Разраб.		Кырлан А.С.			18.10.26
Пров.					
ГИП					
Н. контр.					
Утв.					

ГД-2026-009-АИ

Квартира 103 м²

Общая площадь 100,72* м² · * размеры со скана, не замерены (реестр — л. 6, К-1)

Дизайн-проект интерьера

Стадия	Лист	Листов
РП	55	96

Шкаф распашной С2

М 1:20

Кырлан Александр Сергеевич

выпуск 18.10.2026 № 53dc234b8d · стр. 65 из 135

Шкаф распашной М4

Спальня мастер (пом. 10) · вид из помещения · размеры в мм, отметки в м

ПРЕДВАРИТЕЛЬНО · не для производства работ · открыто пунктов: 4 (реестр — л. 6)

Вид с фасадами

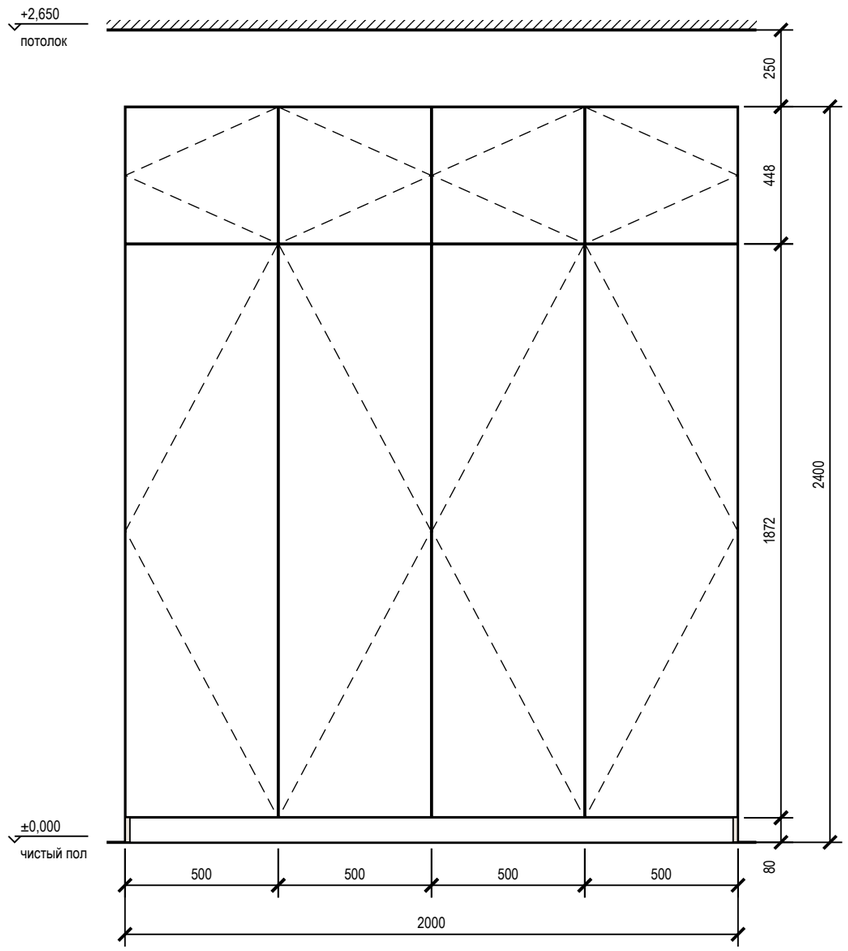

Вид без фасадов

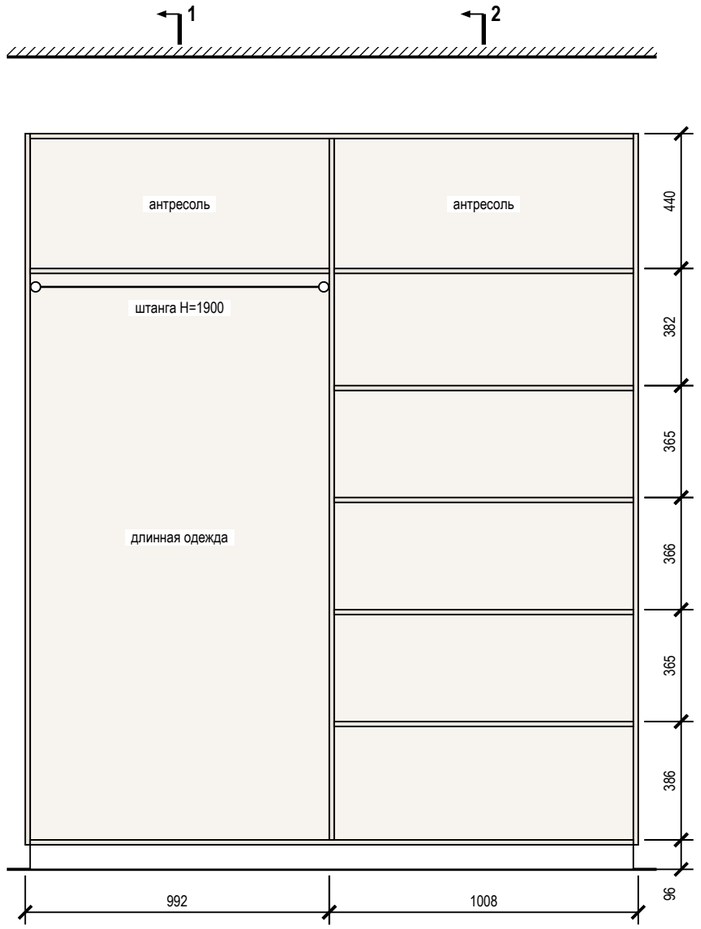

Разрез 1-1

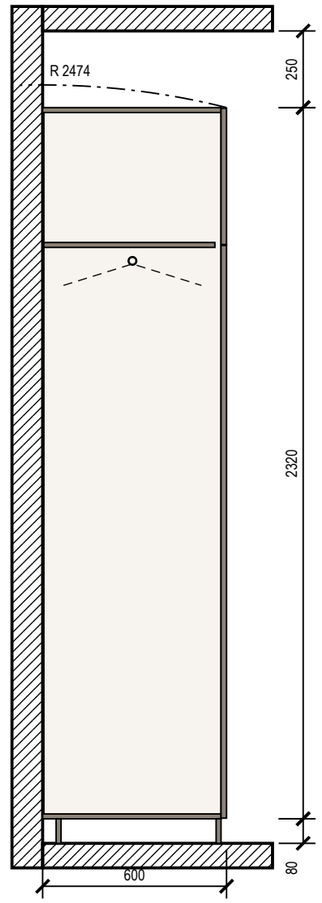

Разрез 2-2

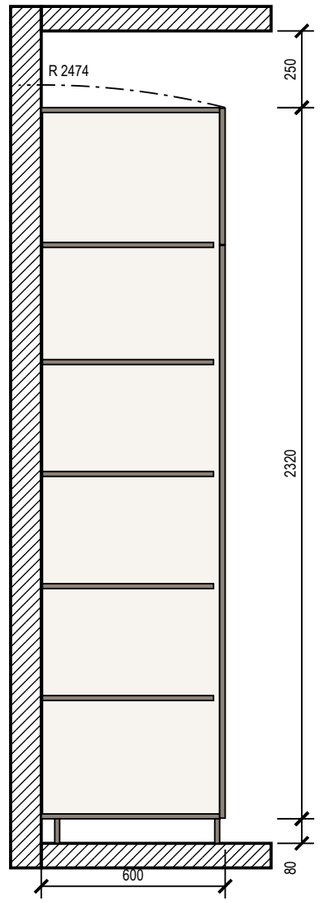

Примечания

1. Размеры — в мм по чистовой отделке; изделие 2000×600×2400 (Ш×Г×В). Перед раскроем — контрольный замер цеха после чистовой отделки стен, пола и потолка.
2. Корпус — ЛДСП 16 мм, задняя стенка ХДФ 4 мм в паз, цоколь 80 мм на регулируемых опорах; фасады — МДФ, эмаль матовая 18 мм накладные, цвет — по колерной карте; петли с доводчиком: фасад 1869 мм — 4 петли, фасад 445 мм — 2 петли.
3. Кромка: скрытые торцы 0,4 мм, видимые 2 мм (ПВХ/АБС).
4. Номинальные зазоры: между фасадами 3 мм, фасад — стена и фасад — потолок не менее 3 мм, фасад ящика — стойка 2 мм.
5. Ящики — направляющие полного выдвижения NL 550 (внутренняя глубина 578 мм ≥ NL + 3); присадка по 32-й системе — выполняет цех.
6. Зазор до потолка 250 мм.
7. Подъём корпуса: диагональ боковины $\sqrt{(2400^2 + 600^2)}$ = 2474 мм < 2650 мм до потолка — корпус собирается лёжа и поднимается поворотом.
8. Крепление к стене от опрокидывания — уголки 2 шт. к несущему основанию (монтажная схема шкафов).

Условные обозначения

- фасад распашной: линии сходятся к стороне петель
- корпус и полки ЛДСП (вид на стену)
- задняя стенка ХДФ
- деталь в разрезе
- штанга для плечиков (на разрезе — плечики 450 мм)
- траектория угла корпуса при подъёме в проектное положение

Допущения и предложения на листе

Основа листа: размеры сняты со скана обмерного плана KV design (см): часть подписей не читается, помещения выровнены по читаемым размерам; контрольный обмер не выполнен (К-1); высота потолка 2650 мм принята по отметкам обмера (Н = 2,50…2,66 м, ригель 2,28 м) — уточнить при обмере (К-2); толщины стен 300 / 120 мм приняты, межквартирная стена и колонны — по скану, не замерены (К-1); разрешённая мощность 15 кВт принята по типовым ТУ; при объединении двух квартир — переоформление ТУ (К-4).
См. лист открытых вопросов (лист 6, записи К-1, К-2, К-4).

1000 мм · печать 1:1

Изм.	Кол.уч	Лист	№ док.	Подп.	Дата
Разраб.		Кырлан А.С.			18.10.26
Пров.					
ГИП					
Н. контр.					
Утв.					

ГД-2026-009-АИ

Квартира 103 м²

Общая площадь 100,72* м² · * размеры со скана, не замерены (реестр — л. 6, К-1)

Дизайн-проект интерьера

Стадия	Лист	Листов
РП	56	96

Шкаф распашной М4

М 1:20

Кырлан Александр Сергеевич

выпуск 18.10.2026 № 53dc234b8d · стр. 66 из 135

Кухня (пом. 5). Развёртка гарнитура

Кухня (пом. 5) · стена Б · вид из помещения · размеры в мм, отметки в м

ПРЕДВАРИТЕЛЬНО · не для производства работ · открыто пунктов: 4 (реестр — л. 6)

Вид с фасадами

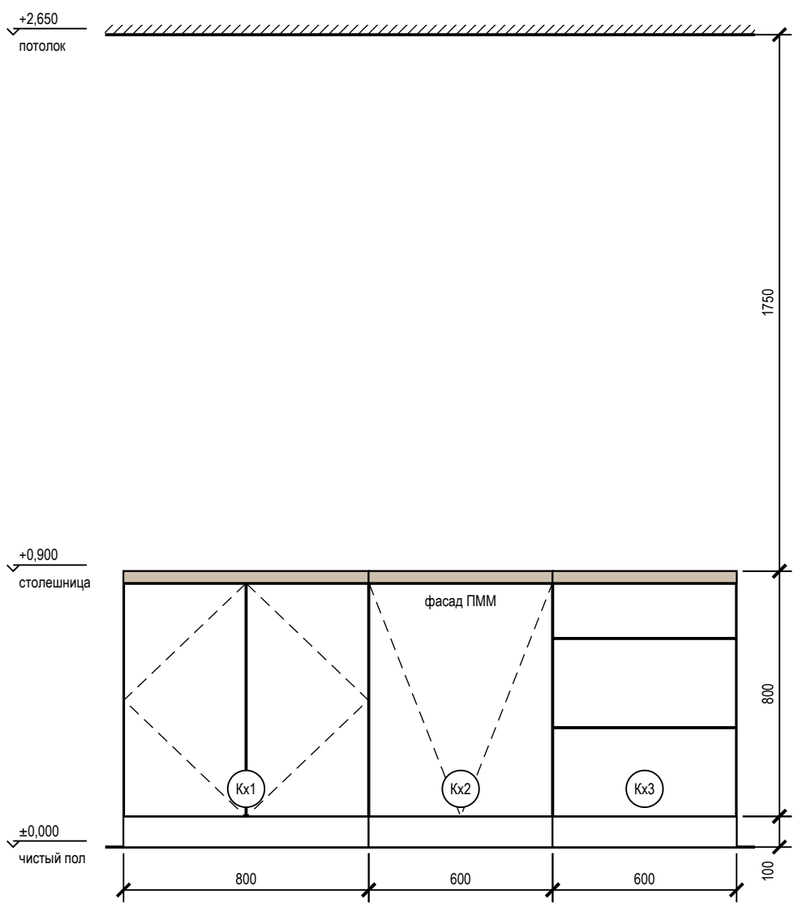

Вид без фасадов (наполнение, выводы)

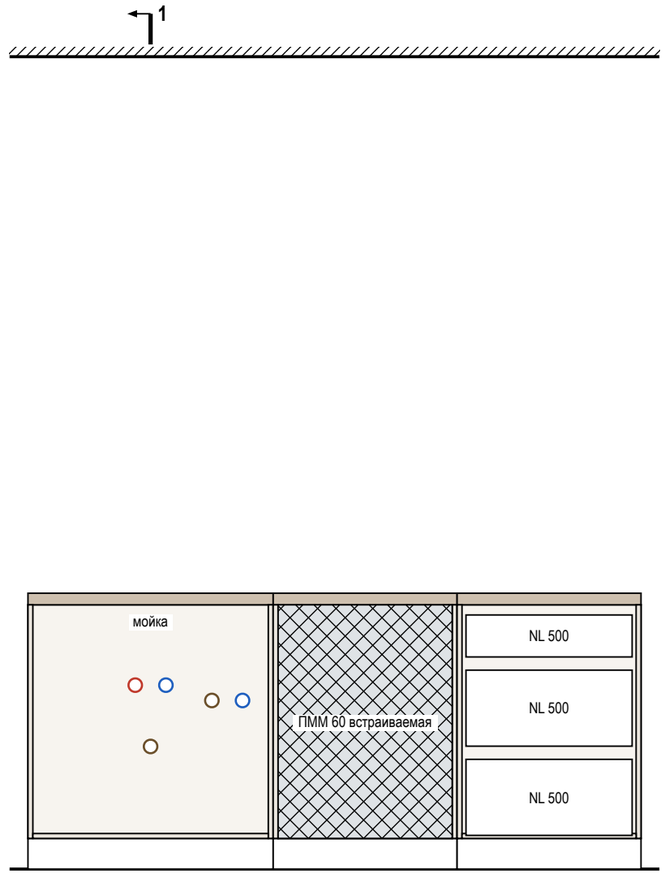

Разрез 1-1

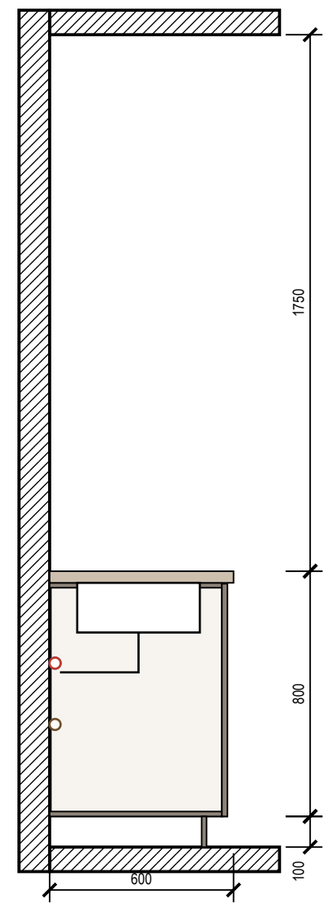

Условные обозначения

- фасад распашной: линии сходятся к стороне петель
- фасад ящика, карго
- встраиваемая техника
- столешница
- доборная планка
- деталь в разрезе
- К1 — марка модуля
- розетка на стене
- вывод кабеля к технике
- В1 — вывод воды В1 / Т3, канализации К1

Допущения и предложения на листе

Основа листа: размеры сняты со скана обмерного плана KV design (см): часть подписей не читается, помещения выровнены по читаемым размерам; контрольный обмер не выполнен (К-1); высота потолка 2650 мм принята по отметкам обмера (Н = 2,50…2,66 м, ригель 2,28 м) — уточнить при обмере (К-2); толщины стен 300 / 120 мм приняты, межквартирная стена и колонны — по скану, не замерены (К-1); разрешённая мощность 15 кВт принята по типовым ТУ; при объединении двух квартир — переоформление ТУ (К-4).

См. лист открытых вопросов (лист 6, записи К-1, К-2, К-4).

1000 мм · печать 1:1

Примечания

1. Размеры — в мм по чистовой отделке, вид из помещения; марки — как на плане расстановки. Перед раскроем — контрольный замер цеха после фартука и пола.
2. Корпуса — ЛДСП 16 мм, задняя стенка ХДФ 4 мм; фасады — МДФ, эмаль матовая 18 мм, цвет по колерной карте; столешница 38 мм, свес 20 мм; цоколь 100 мм.
3. Кромка: скрытые торцы 0,4 мм, видимые 2 мм. Номинальные зазоры: между фасадами 3 мм, фасад — столешница 3 мм, фасад — стена не менее 3 мм.
4. Ящики полного выдвижения и петли — с доводчиком; присадка по 32-й системе — выполняет цех.
5. Ниши техники — по монтажным схемам выбранных моделей: решётка в цоколе и канал за пеналом холодильника, зазор за духовым шкафом, фасад ПММ на двери машины.

Изм.	Кол.уч	Лист	№ док.	Подп.	Дата
Разраб.		Кырлан А.С.			18.10.26
Пров.					
ГИП					
Н. контр.					
Утв.					

ГД-2026-009-АИ

Квартира 103 м²

Общая площадь 100,72* м² · * размеры со скана, не замерены (реестр — л. 6, К-1)

Дизайн-проект интерьера	Стадия	Лист	Листов
	РП	57	96

Кухня (пом. 5). Развёртка гарнитура

М 1:20

Кырлан Александр Сергеевич

выпуск 18.10.2026 № 53dc234b88d · стр. 67 из 135

Кухня (пом. 5). Монтажная схема

Кухня (пом. 5) · стена Б · размеры в мм от чистых поверхностей, высоты — от чистого пола

ПРЕДВАРИТЕЛЬНО · не для производства работ · открыто пунктов: 4 (реестр — л. 6)

Привязка выводов и крепление модулей

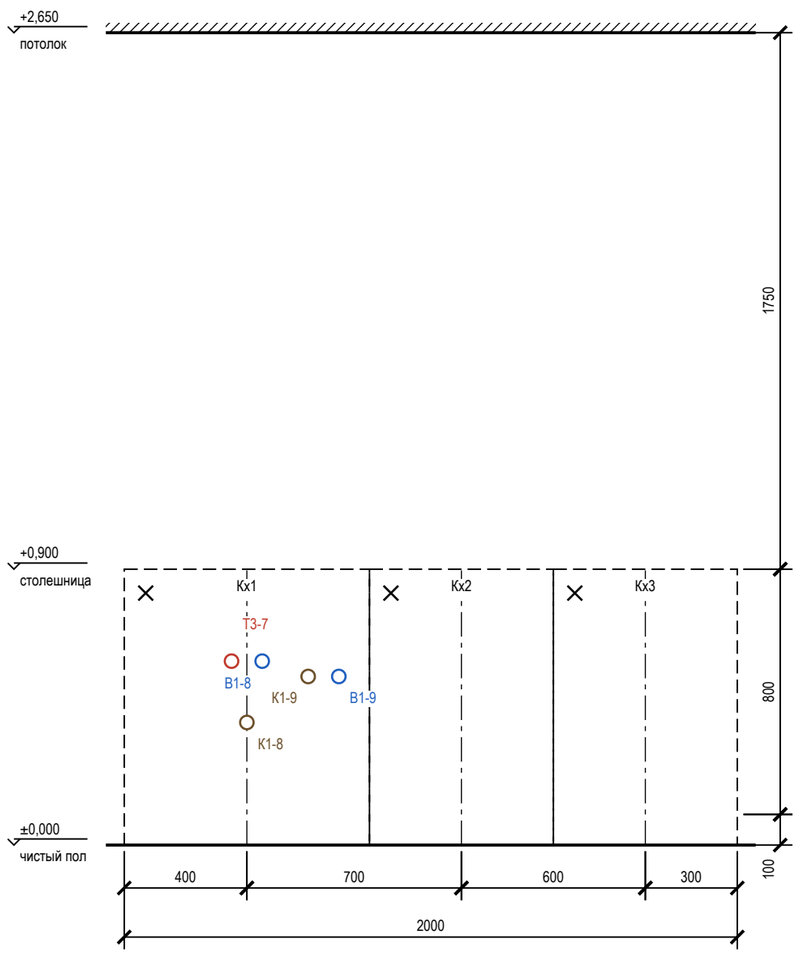

План столешницы

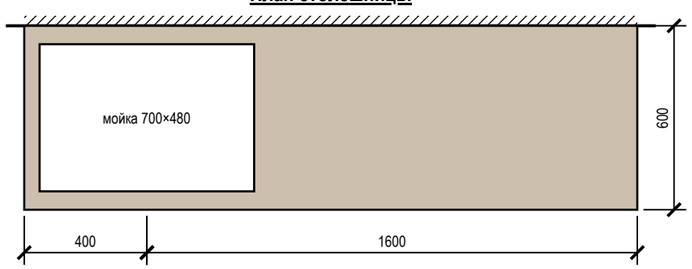

Привязка выводов к осям модулей

Код	Назначение	Модуль	От оси, мм	Н, мм	Размещение
Т3-7	Т3 — межос. 100	Кх1	−50	600	в модуле мойки
К1-8	К1 Ø50 — мойка	Кх1	0	400	в модуле мойки
В1-8	В1 — межос. 100	Кх1	+50	600	в модуле мойки
К1-9	К1 Ø40 — слив ПММ в шкафу мойки	Кх1	+200	550	в модуле мойки
В1-9	В1 — кран ПММ в шкафу мойки	Кх1	+300	550	в модуле мойки

Зазоры под отделку

Поверхность	Отделка	Зазор, мм	Учесть
фартук	керамогранит	10	от чернового основания до корпуса навесных и столешницы
стены	окраска	5	под штукатурку и шпаклёвку за пеналом
пол	инженерная доска		цоколь — после укладки пола, опоры ±20 мм

Условные обозначения

- навесной модуль (невидимый контур)
- ось модуля (от неё — привязка вывода)
- анкер / уголок крепления к стене
- розетка на стене
- вывод кабеля к технике
- В1 — вывод воды В1 / Т3, канализации К1

Примечания

1. Выводы — по проекту электрики и ВК; привязка по горизонтали — от оси модуля (плюс — вправо по виду), по высоте — от чистого пола до оси вывода.
2. Пенал — уголки к стене 2 шт. сверху; нижние модули — стяжками между собой и уголком к стене; ряд выставить по уровню опорами цоколя.
3. Розетки над столешницей — не ниже 150 мм над ней и не за корпусом техники; розетка за ПММ, духовым шкафом и холодильником — только в соседнем модуле или в зоне цоколя с доступом.
4. Столешница — вырезы по шаблонам выбранных моделей мойки и варочной панели; торцы у стены — герметик, пристеночный плинтус.

Допущения и предложения на листе

Основа листа: размеры сняты со скана обмерного плана KV design (см): часть подписей не читается, помещения выровнены по читаемым размерам; контрольный обмер не выполнен (К-1); высота потолка 2650 мм принята по отметкам обмера (Н = 2,50…2,66 м, ригель 2,28 м) — уточнить при обмере (К-2); толщины стен 300 / 120 мм приняты, межквартирная стена и колонны — по скану, не замерены (К-1); разрешённая мощность 15 кВт принята по типовым ТУ; при объединении двух квартир — переоформление ТУ (К-4).
См. лист открытых вопросов (лист 6, записи К-1, К-2, К-4).

1000 мм · печать 1:1

Изм.	Кол.уч	Лист	№ док.	Подп.	Дата
Разраб.		Кырлан А.С.			18.10.26
Пров.					
ГИП					
Н. контр.					
Утв.					

ГД-2026-009-АИ

Квартира 103 м²

Общая площадь 100,72* м² · * размеры со скана, не замерены (реестр — л. 6, К-1)

Дизайн-проект интерьера

Стадия	Лист	Листов
РП	58	96

Кухня (пом. 5). Монтажная схема

М 1:20

Кырлан Александр Сергеевич

выпуск 18.10.2026 № 53dc2340b8d · стр. 68 из 135

Кухня (пом. 5). Развёртка гарнитура

Кухня (пом. 5) · стена В · вид из помещения · размеры в мм, отметки в м

ПРЕДВАРИТЕЛЬНО · не для производства работ · открыто пунктов: 4 (реестр — л. 6)

Вид с фасадами

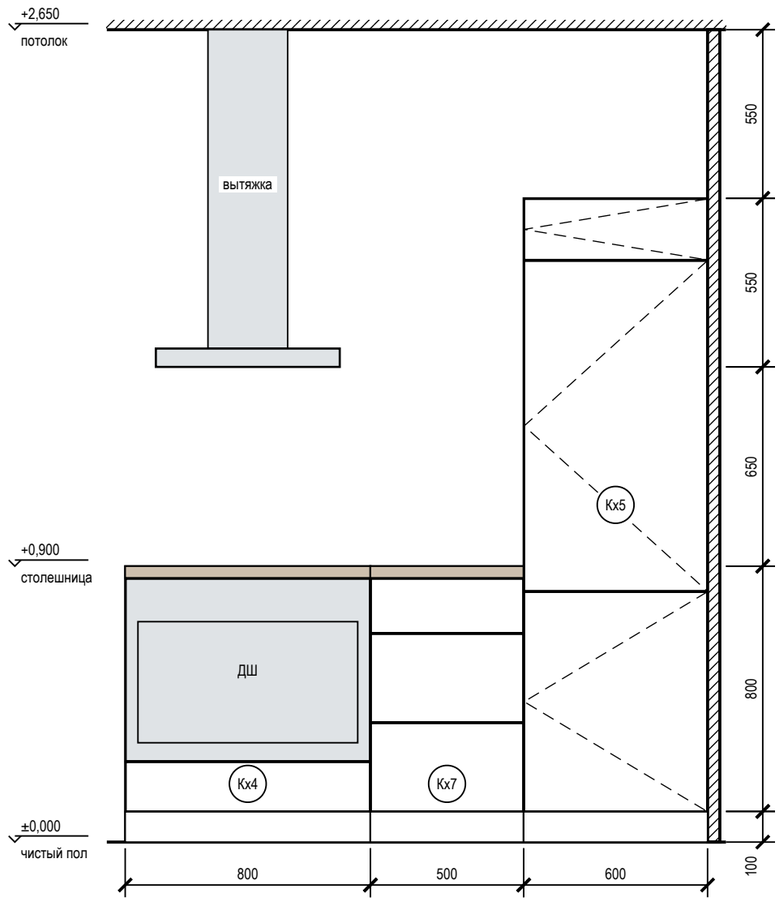

Вид без фасадов (наполнение, выводы)

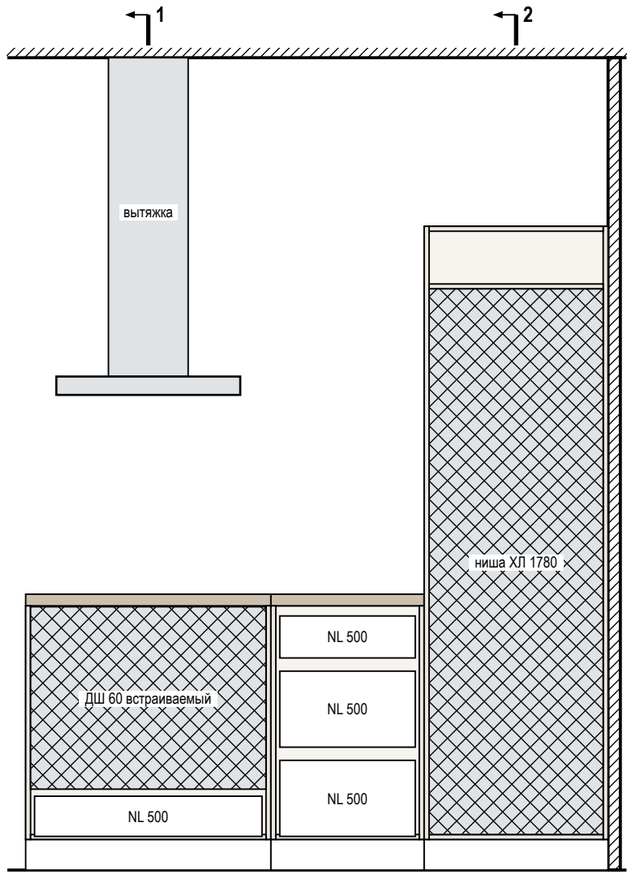

Разрез 1-1

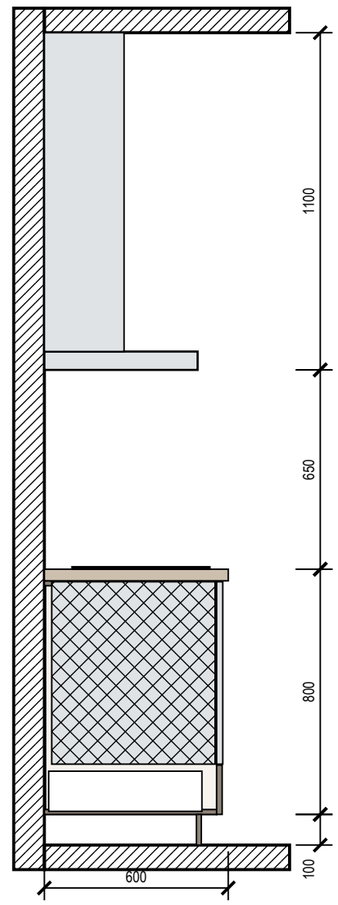

Разрез 2-2

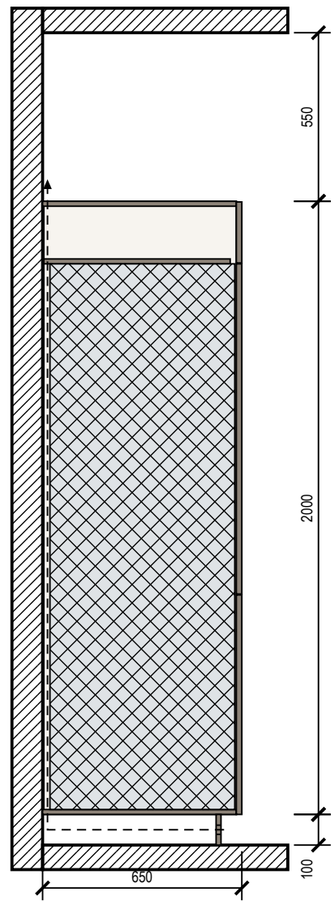

Условные обозначения

- фасад распашной: линии сходятся к стороне петель
- фасад ящика, карго
- встраиваемая техника
- столешница
- доборная планка
- деталь в разрезе
- К1 — марка модуля
- розетка на стене
- вывод кабеля к технике
- В1 — вывод воды В1 / Т3, канализации К1

Допущения и предложения на листе

Основа листа: размеры сняты со скана обмерного плана KV design (см): часть подписей не читается, помещения выровнены по читаемым размерам; контрольный обмер не выполнен (К-1); высота потолка 2650 мм принята по отметкам обмера (Н = 2,50…2,66 м, ригель 2,28 м) — уточнить при обмере (К-2); толщины стен 300 / 120 мм приняты, межквартирная стена и колонны — по скану, не замерены (К-1); разрешённая мощность 15 кВт принята по типовым ТУ; при объединении двух квартир — переоформление ТУ (К-4).
См. лист открытых вопросов (лист 6, записи К-1, К-2, К-4).

1000 мм · печать 1:1

Примечания

1. Размеры — в мм по чистовой отделке, вид из помещения; марки — как на плане расстановки. Перед раскроем — контрольный замер цеха после фартука и пола.
2. Корпуса — ЛДСП 16 мм, задняя стенка ХДФ 4 мм; фасады — МДФ, эмаль матовая 18 мм, цвет по колерной карте; столешница 38 мм, свес 20 мм; цоколь 100 мм.
3. Кромка: скрытые торцы 0,4 мм, видимые 2 мм. Номинальные зазоры: между фасадами 3 мм, фасад — столешница 3 мм, фасад — стена не менее 3 мм.
4. Ящики полного выдвижения и петли — с доводчиком; присадка по 32-й системе — выполняет цех.
5. Низ вытяжки — не ниже 650 мм над варочной панелью или по паспорту модели; короб воздуховода — до потолка.
6. Ниши техники (холодильник — ориентир 1780 мм) — по монтажным схемам выбранных моделей: решётка в цоколе и канал за пеналом холодильника, зазор за духовым шкафом, фасад ПММ на двери машины.

Изм.	Кол.уч	Лист	№ док.	Подп.	Дата
Разраб.		Кырлан А.С.			18.10.26
Пров.					
ГИП					
Н. контр.					
Утв.					

ГД-2026-009-АИ

Квартира 103 м²

Общая площадь 100,72* м² · * размеры со скана, не замерены (реестр — л. 6, К-1)

Дизайн-проект интерьера

Стадия	Лист	Листов
РП	59	96

Кухня (пом. 5). Развёртка гарнитура

М 1:20

Кырлан Александр Сергеевич

выпуск 18.10.2026 № 53dc234b8d · стр. 69 из 135

Кухня (пом. 5). Монтажная схема

Кухня (пом. 5) · стена В · размеры в мм от чистых поверхностей, высоты — от чистого пола

ПРЕДВАРИТЕЛЬНО · не для производства работ · открыто пунктов: 4 (реестр — л. 6)

Привязка выводов и крепление модулей

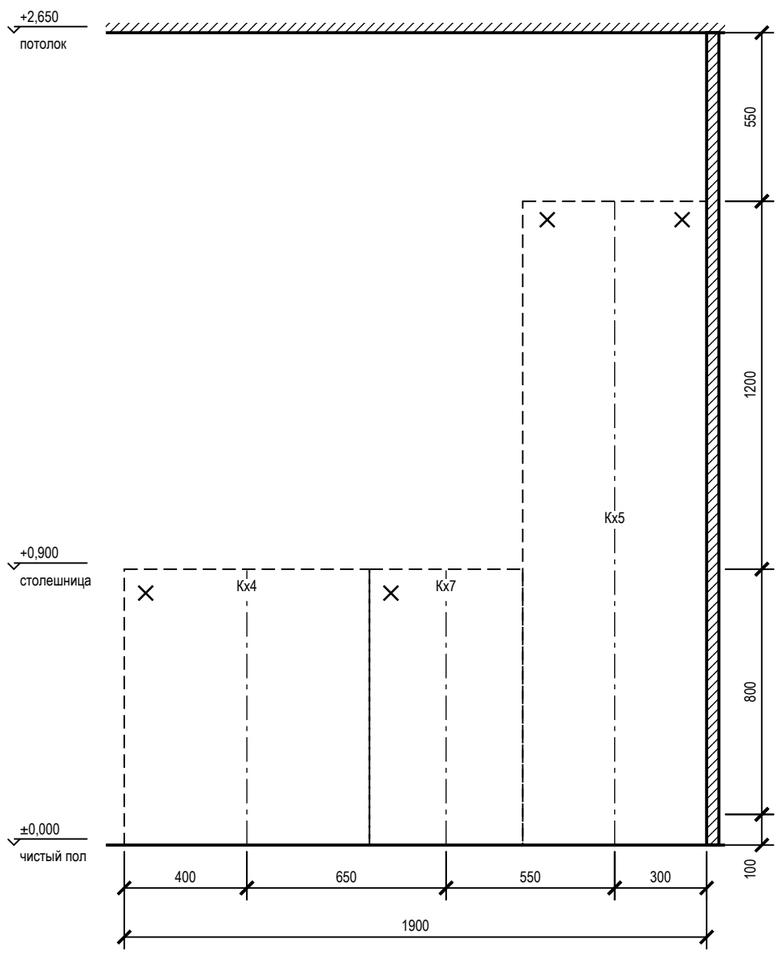

План столешницы

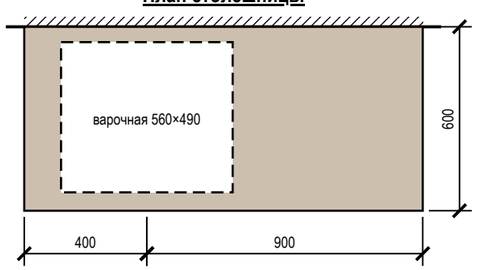

Привязка выводов к осям модулей

Код	Назначение	Модуль	От оси, мм	Н, мм	Размещение

Зазоры под отделку

Поверхность	Отделка	Зазор, мм	Учесть
фартук	керамогранит	10	от чернового основания до корпуса навесных и столешницы
стены	окраска	5	под штукатурку и шпаклёвку за пеналом
пол	инженерная доска		цоколь — после укладки пола, опоры ±20 мм

Условные обозначения

- навесной модуль (невидимый контур)
- ось модуля (от неё — привязка вывода)
- анкер / уголок крепления к стене
- розетка на стене
- вывод кабеля к технике
- B1 — вывод воды В1 / Т3, канализации К1

Допущения и предложения на листе

Основа листа: размеры сняты со скана обмерного плана KV design (см): часть подписей не читается, помещения выровнены по читаемым размерам; контрольный обмер не выполнен (К-1); высота потолка 2650 мм принята по отметкам обмера (Н = 2,50…2,66 м, ригель 2,28 м) — уточнить при обмере (К-2); толщины стен 300 / 120 мм приняты, межквартирная стена и колонны — по скану, не замерены (К-1); разрешённая мощность 15 кВт принята по типовым ТУ; при объединении двух квартир — переоформление ТУ (К-4).
См. лист открытых вопросов (лист 6, записи К-1, К-2, К-4).

Примечания

1. Выводы — по проекту электрики и ВК; привязка по горизонтали — от оси модуля (плюс — вправо по виду), по высоте — от чистого пола до оси вывода.
2. Пенал — уголки к стене 2 шт. сверху; нижние модули — стяжками между собой и уголком к стене; ряд выставить по уровню опорами цоколя.
3. Розетки над столешницей — не ниже 150 мм над ней и не за корпусом техники; розетка за ПММ, духовым шкафом и холодильником — только в соседнем модуле или в зоне цоколя с доступом.
4. Столешница — вырезы по шаблонам выбранных моделей мойки и варочной панели; торцы у стены — герметик, пристеночный плинтус.

1000 мм · печать 1:1

Изм.	Кол.уч	Лист	№ док.	Подп.	Дата
Разраб.		Кырлан А.С.			18.10.26
Пров.					
ГИП					
Н. контр.					
Утв.					

ГД-2026-009-АИ

Квартира 103 м²

Общая площадь 100,72* м² · * размеры со скана, не замерены (реестр — л. 6, К-1)

Дизайн-проект интерьера

Стадия	Лист	Листов
РП	60	96

Кухня (пом. 5). Монтажная схема

М 1:20

Кырлан Александр Сергеевич

выпуск 18.10.2026 № 53dc234b8d · стр. 70 из 135

Шкафы. Монтажная схема

крепление к стене, установочные размеры, зазоры под отделку · размеры в мм

ПРЕДВАРИТЕЛЬНО · не для производства работ · открыто пунктов: 4 (реестр — л. 6)

Система хранения К1 (пом. 2)

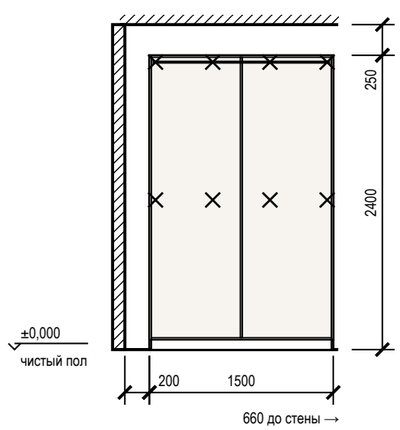

Шкаф-купе П1 (пом. 4)

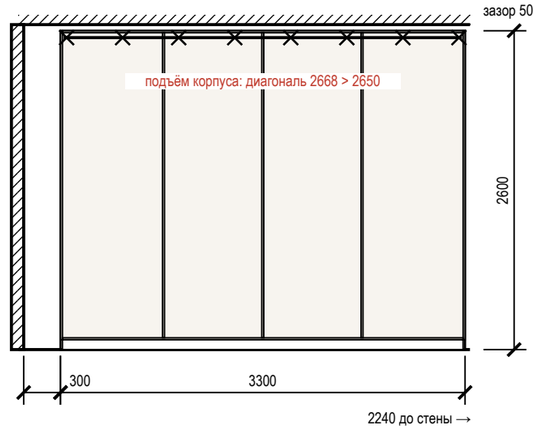

Система хранения Пс1 пом. 7

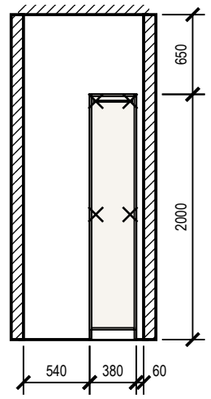

Шкаф распашной С2 (пом. 8)

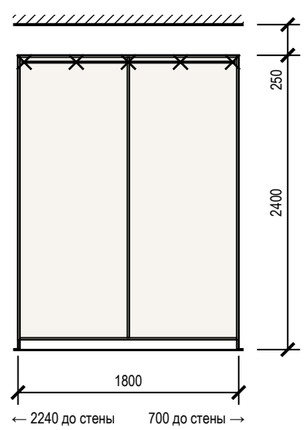

Шкаф распашной М4 (пом. 10)

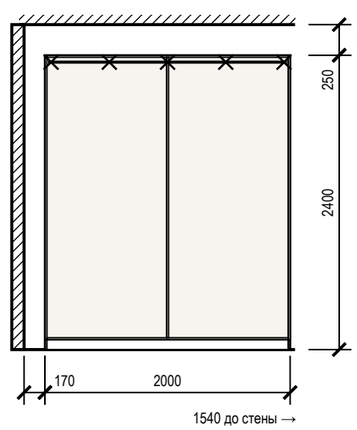

Крепление и зазоры под отделку

Марка	Помещение, стена	Основание	Отделка стены	Зазор, мм	Крепёж по планке	От опрокидывания
К1	Кладовая (2), стена Б	по основанию — см. таблицу крепежа	окраска	5	анкер 8 шт. (2 ряда)	уголки 2 шт.
П1	Прихожая-холл (4), стена А	по основанию — см. таблицу крепежа	окраска	5	анкер 8 шт., шаг 457	уголки 2 шт.
Пс1	Постирочная (7), стена А	по основанию — см. таблицу крепежа	окраска	5	анкер 4 шт. (2 ряда)	уголки 2 шт.
С2	Спальня 2 (8), стена А	по основанию — см. таблицу крепежа	окраска	5	анкер 5 шт., шаг 425	уголки 2 шт.
М4	Спальня мастер (10), стена Г	по основанию — см. таблицу крепежа	окраска	5	анкер 5 шт., шаг 475	уголки 2 шт.

Крепёж по основанию стены

Основание стены	Крепёж
бетон, ж/б	анкер-шуруп 7,5×72 или дюбель 8×60 с шурупом 5×70
кирпич полнотелый	дюбель 8×80 с шурупом 5×90
газобетон, пазогребень	дюбель для газобетона 10×100 или химический анкер
гипсокартон	закладная до обшивки (брус 40×80 или фанера 18 мм), саморез в закладную

Условные обозначения

- анкер / уголок крепления к стене
- корпус и полки ЛДСП (вид на стену)
- компенсатор — короб до потолка

Примечания

1. Установочные размеры — от чистого пола и чистых стен; перед установкой контрольный замер после отделки.
2. Порядок: корпус выставить по уровню опорами цоколя → закрепить к стене по задней планке → навесить двери и фасады, отрегулировать зазоры → подогнать и закрепить компенсатор.
3. Анкеры — с шагом не более 500 мм, не ближе 50 мм от края планки; на ГКЛ только в закладную, установленную до обшивки.
4. Скрытые коммуникации под анкеры проверить детектором; трассы электрики по плану розеток.

Допущения и предложения на листе

Основа листа: размеры сняты со скана обмерного плана KV design (см): часть подписей не читается, помещения выровнены по читаемым размерам; контрольный обмер не выполнен (К-1); высота потолка 2650 мм принята по отметкам обмера (Н = 2,50…2,66 м, ригель 2,28 м) — уточнить при обмере (К-2); толщины стен 300 / 120 мм приняты, межквартирная стена и колонны — по скану, не замерены (К-1); разрешённая мощность 15 кВт принята по типовым ТУ; при объединении двух квартир — переоформление ТУ (К-4).
См. лист открытых вопросов (лист 6, записи К-1, К-2, К-4).

1000 мм · печать 1:1

Изм.	Кол.уч	Лист	№ док.	Подп.	Дата
Разраб.		Кырлан А.С.			18.10.26
Пров.					
ГИП					
Н. контр.					
Утв.					

ГД-2026-009-АИ

Квартира 103 м²

Общая площадь 100,72* м² · * размеры со скана, не замерены (реестр — л. 6, К-1)

Дизайн-проект интерьера

Стадия	Лист	Листов
РП	61	96

Шкафы. Монтажная схема

М 1:50

Кырлан Александр Сергеевич

выпуск 18.10.2026 № 53dc234b8d · стр. 71 из 135

Ведомости изделий, техники и фурнитуры

встроенная мебель и кухонный гарнитур · размеры в мм

Ведомость изделий

Марка	Наименование	Пом.	Ш×Г×В, мм	Корпус	Фасад	Кромка, мм скр./вид.	Кол.
К1	Система хранения	2	1500×400×2400	ЛДСП 16	без фасадов; ящики — МДФ 18, эмаль матовая	0,4 / 2	1
П1	Шкаф-купе	4	3300×600×2600	ЛДСП 16	рифлёные панели МДФ в алюминиевом профиле	0,4 / 2	1
Пс1	Система хранения	7	380×350×2000	ЛДСП 16	без фасадов; ящики — МДФ 18, эмаль матовая	0,4 / 2	1
С2	Шкаф распашной	8	1800×600×2400	ЛДСП 16	МДФ 18, эмаль матовая	0,4 / 2	1
М4	Шкаф распашной	10	2000×600×2400	ЛДСП 16	МДФ 18, эмаль матовая	0,4 / 2	1
Кх1	Модуль нижний: мойка	5	800×600×900	ЛДСП 16	МДФ 18, эмаль матовая	0,4 / 2	1
Кх2	Модуль нижний: ПММ	5	600×600×900	ЛДСП 16	МДФ 18, эмаль матовая	0,4 / 2	1
Кх3	Модуль нижний: ящики	5	600×600×900	ЛДСП 16	МДФ 18, эмаль матовая	0,4 / 2	1
Кх4	Модуль нижний: духовой шкаф, варочная	5	800×600×900	ЛДСП 16	МДФ 18, эмаль матовая	0,4 / 2	1
Кх7	Модуль нижний: ящики	5	500×600×900	ЛДСП 16	МДФ 18, эмаль матовая	0,4 / 2	1
Кх5	Пенал: холодильник встр.	5	600×650×2100	ЛДСП 16	МДФ 18, эмаль матовая	0,4 / 2	1

Ведомость встраиваемой техники

Поз.	Прибор	Ниша, вырез, мм	Вентиляция	Питание	Схема
Кх1	Мойка врезная / подстольная с сифоном	вырез по шаблону, ориентир 700 × 480		смеситель — выводы ВК	по модели
Кх2	Посудомоечная машина встраиваемая, 60 см	ниша 600 × 862 (от пола до низа столешницы)	зазор в цоколе, по схеме	розетка в соседнем модуле	по модели
Кх4	Духовой шкаф встраиваемый, 60 см	ниша 560 × 595, глубина ≥ 550	зазор за шкафом, вырез в задней стенке	вывод кабеля под шкафом	по модели
Кх4	Варочная панель индукционная, 60 см	вырез в столешнице 560 × 490		вывод кабеля под модулем	по модели
Кх5	Холодильник встраиваемый, ниша 1780	ниша 1780 × 560 × 550	решётка в цоколе, канал за корпусом, выход сверху	розетка над нишей или в соседнем модуле	по модели
Кх4	Вытяжка настенная, 60 см	низ ≥ 650 над панелью	воздуховод к вентканалу, короб до потолка	вывод кабеля в коробе	по модели

Ведомость фурнитуры

№	Фурнитура	Тип, размер	Изделия	Кол.
1	Полкодержатель с фиксацией	ø5 мм	К1, П1, С2, М4, Кх5	132
2	Штанга выдвижная торцевая	L по глубине	К1, Пс1	2
3	Опора регулируемая с цоколем на клипсах	ход 20 мм	К1, П1, Пс1, С2, М4	38
4	Анкер по основанию стены	по таблице крепежа	К1, П1, Пс1, С2, М4	30
5	Уголок крепления к стене от опрокидывания	стальной	К1, П1, Пс1, С2, М4, Кх5	12
6	Система дверей купе: профиль, направляющие, ролики	на 4 двери	П1	1
7	Ручка-профиль вертикальная	в цвет профиля	П1	4
8	Штанга овальная 30×15, L = 817	+ 2 держателя	П1	1
9	Полка для обуви выдвижная наклонная	ширина 817	П1	3
10	Полка для обуви выдвижная наклонная	ширина 794	П1	3
11	Штанга овальная 30×15, L = 794	+ 2 держателя	П1	1
12	Петля накладная 110° с доводчиком	чашка 35 мм	С2, М4, Кх1, Кх5	59
13	Штанга овальная 30×15, L = 876	+ 2 держателя	С2	1
14	Штанга овальная 30×15, L = 976	+ 2 держателя	М4	1
15	Ручка-профиль	латунь матовая	Кх1, Кх2, Кх3, Кх4, Кх7, Кх5	13
16	Опора кухонная регулируемая 100–120 мм	+ клипса цоколя	Кх1, Кх2, Кх3, Кх4, Кх7, Кх5	28
17	Комплект навески фасада ПММ	из поставки машины	Кх2	1
18	Направляющие полного выдвижения с доводчиком NL 500	пара	Кх3, Кх4, Кх7	7

Примечания

1. Модели техники выбирает заказчик до изготовления мебели; ниши, вырезы и вентиляция — по монтажной схеме выбранной модели (условие гарантии), её номер вносится в ведомость.
2. Количество фурнитуры — по чертежам изделий; запас крепежа 5 %. Аналоги — по характеристикам (доводчик, нагрузка, ход).
3. Цвет корпусов, фасадов и профилей — по колерной карте проекта.

Допущения и предложения на листе

Основа листа: размеры сняты со скана обмерного плана KV design (см): часть подписей не читается, помещения выровнены по читаемым размерам; контрольный обмер не выполнен (К-1); высота потолка 2650 мм принята по отметкам обмера (Н = 2,50…2,66 м, ригель 2,28 м) — уточнить при обмере (К-2); толщины стен 300 / 120 мм приняты, межквартирная стена и колонны — по скану, не замерены (К-1); разрешённая мощность 15 кВт принята по типовым ТУ; при объединении двух квартир — переоформление ТУ (К-4).
См. лист открытых вопросов (лист 6, записи К-1, К-2, К-4).

Изм.	Кол.уч	Лист	№ док.	Подп.	Дата
Разраб.		Кырлан А.С.			18.10.26
Пров.					
ГИП					
Н. контр.					
Утв.					

ГД-2026-009-АИ

Квартира 103 м²

Общая площадь 100,72* м² · * размеры со скана, не замерены (реестр — л. 6, К-1)

Дизайн-проект интерьера

Стадия	Лист	Листов
РП	62	96

Ведомости изделий, техники и фурнитуры

М б/м

Кырлан Александр Сергеевич

09

Развёртки и узлы

Кырлан Александр Сергеевич

выпуск 18.10.2026 № 53dc234b8d · стр. 73 из 135

Реестр марок отделки и позиций альбома

Реестр марок отделки (О ↔ позиции колерной карты) и марки позиций по видам

ПРЕДВАРИТЕЛЬНО · не для производства работ · открыто пунктов: 4 (реестр — л. 6)

Реестр марок отделки альбома

Марка	Поверхность	Материал, изделие	Цвет, код	Помещения	Колер. карта
О1	стены	окраска, Farrow & Ball Modern Emulsion, матовая, подготовка Q3	Farrow & Ball No. 291 «School House White тёплый меловой белый»	1, 4, 8, 9, 10	К1
О2	акцентная стена	окраска, Farrow & Ball Modern Emulsion, матовая, подготовка Q3	Farrow & Ball No. 289 «Inchyra Blue — тёмный сине-серый»	1, 8, 10	К2
О3	плинтус	плинтус МДФ, h 80 мм, аналог: плинтус МДФ под покраску 80×16	Farrow & Ball No. 291 «School House White тёплый меловой белый»	1, 4, 8, 9, 10	К4
О4	потолок	окраска, Tikkurila Anti-Reflex 2, глубокоматовая, подготовка Q3	NCS S 0502-Y «Белый с лёгкой желтизной»	1, 2, 4, 7, 8, 9, 10	К3
О5	пол	инженерная доска, Coswick Вековые традиции, 2100×127 мм, 1167-4250		1, 2, 3, 5, 7, 8, 9, 10	КМ1
О6	стены	окраска, Tikkurila Harmony, матовая, подготовка Q3	NCS S 0502-Y «Белый с лёгкой желтизной»	2, 7	К5
О7	плинтус	плинтус МДФ, h 80 мм, аналог: плинтус МДФ под покраску 80×16	NCS S 0502-Y «Белый с лёгкой желтизной»	2, 7	К6
О8	стены	окраска, Tikkurila Optiva 5 Matt, матовая, подготовка К3	Farrow & Ball No. 291 «School House White тёплый меловой белый»	3	К7
О9	акцентная стена	окраска, Tikkurila Optiva 5 Matt, аналог: интерьерная краска, класс 2 по EN 13300, глубокоматовая/матовая, база С, матовая, подготовка К3	Farrow & Ball No. 255 «Tanner's Brown тёмный шоколад»	3	К8
О10	плинтус	плинтус МДФ, h 80 мм, аналог: плинтус МДФ под окраску 80×16 мм, полуглянцевая	Farrow & Ball No. 291 «School House White тёплый меловой белый»	3, 5	К10
О11	потолок	окраска, Tikkurila Anti-Reflex 2, глубокоматовая, подготовка Q3	Farrow & Ball No. 291 «School House White тёплый меловой белый»	3	К9
О12	пол	керамогранит, Atlas Concorde Marvel Travertine, 600×1200×9 мм, A8UZ, затирка CG2WA	Atlas Concorde A8UZ «Marvel Travertine»	4, 6, 11	К11
О13	стены	окраска, Tikkurila Luja 7, шелковисто-матовая, подготовка К3	Farrow & Ball No. 291 «School House White тёплый меловой белый»	5	К12
О14	фартук	керамогранит, аналог: керамогранит матовый, тон F497, затирка CG2WA	#F1F1EC «тон Paper F497»	5	КМ2
О15	потолок	окраска, Tikkurila Luja 7, матовая, подготовка Q3	Farrow & Ball No. 291 «School House White тёплый меловой белый»	5	К13
О16	стены	облицовка плиткой, Atlas Concorde Marvel Travertine, 600×1200×9 мм, A8UZ, затирка CG2WA	Atlas Concorde A8UZ «Marvel Travertine»	6, 11	К11
О17	потолок	окраска, Tikkurila Luja 7, матовая, подготовка Q3	NCS S 0502-Y «Белый с лёгкой желтизной»	6, 11	К14

Марки позиций альбома по видам

Префикс	Что обозначает, позиции	Листы
Д	двери: Д-1–Д-9	12–14
ПР	проёмы без полотна (порталы): ПР-1	12–14

Марки позиций альбома по видам (продолжение)

Префикс	Что обозначает, позиции	Листы
ОК	окна: ОК-1–ОК-7	12–14
Б, Г, К, Кх, М, П, Пс, С	мебель и оборудование: Б1–Б4, Г1–Г6, К1, Кх1–Кх7, М1–М6, П1–П3, Пс1, С1–С3	15–19
Пс, См, Сн	сантехнические приборы: Пс2, См1–См3, Сн1–Сн4	30–32
ДК	декор (картины, зеркала, растения): ДК1–ДК9	1, 46–50
Т	текстиль (шторы, ковры): Т1–Т24	1, 46–50
S	выключатели: S1, S2**, S3–S9, S14–S16	20–27
Р	розетки: Р1–Р6, Р7**, Р8**, Р9–Р11, Р12**, Р13–Р16, Р17**, Р18–Р20, Р21**, Р22–Р26, Р33**, Р34	20–27
ТВ	розетки ТВ: ТВ1, ТВ2	20–27
LAN	розетки компьютерные: LAN1, LAN2	20–27
Св	светильники: Св1–Св39, Св50–Св54	20–27
БП	блоки питания LED: БП1–БП3	20–27
ИП	извещатели: ИП1–ИП4, ИП6	20–27
ЩК, ЩС**	щиты: ЩК, ЩС**	20–27
ДФ	домофон: ДФ1	20–27
АР	точки доступа Wi-Fi: АР1**	20–27
ЭВ	выводы кабеля: ЭВ3, ЭВ4**, ЭВ5**, ЭВ6**, ЭВ7**	20–27
КУП	электроустановочные изделия: КУП1**, КУП2**	20–27
Ст В1, Ст К1, Ст К1-2 (кухня), Ст К1-4 (постирочная), Ст Т3	стояки (системы В1, Т3, К1): Ст В1-1, Ст В1-2, Ст В1-3, Ст В1-4, Ст К1-1, Ст К1-2 (кухня), Ст К1-3, Ст К1-4 (постирочная), Ст Т3-1, Ст Т3-2, Ст Т3-3, Ст Т3-4	30–32
О	марки отделки (реестр альбома): О1–О17	2–5, 63–89
К, КМ	позиции колерной карты: К1–К14, КМ1, КМ2	42–45
РО	радиаторы отопления: РО-1–РО-7	28, 29

Допущения и предложения на листе. Основа листа: размеры сняты со скана обмерного плана KV design (см): часть подписей не читается, помещения выровнены по читаемым размерам; контрольный обмер не выполнен (К-1); высота потолка 2650 мм принята по отметкам обмера (Н = 2,50…2,66 м, ригель 2,28 м) — уточнить при обмере (К-2); толщины стен 300 / 120 мм приняты, межквартирная стена и колонны — по скану, не замерены (К-1); разрешённая мощность 15 кВт принята по типовым ТУ; при объединении двух квартир — переоформление ТУ (К-4). Знак «**» — предложено, не утверждено (согласовать): записи в реестре нет: плинтус пом. 1–5, 7–10, акцент пом. 3, фартук пом. 5, Р12, S2, Р17, Р21, Р7, Р8, ЭВ4, КУП1, ЭВ6, Р33, ЭВ5, КУП2, ЭВ7, ЩС, АР1. См. лист открытых вопросов (лист 6, записи К-1, К-2, К-4).

Изм.	Кол.уч	Лист	№ док.	Подп.	Дата
Разраб.		Кырлан А.С.			18.10.26
Пров.					
ГИП					
Н. контр.					
Утв.					

ГД-2026-009-АИ

Квартира 103 м²

Общая площадь 100,72* м² · * размеры со скана, не замерены (реестр — л. 6, К-1)

Дизайн-проект интерьера	Стадия	Лист	Листов
	РП	63	96

Реестр марок отделки и позиций альбома

М б/м

Кырлан Александр Сергеевич

выпуск 18.10.2026 № 53dc234b88d · стр. 74 из 135

Реестр марок отделки и позиций альбома (продолжение)

Реестр марок отделки (О ↔ позиции колерной карты) и марки позиций по видам

Примечания

1. Марка отделки О — одна на весь альбом: одна и та же отделка (материал, изделие, цвет, формат) на всех листах имеет одну марку; на развёртках и планах стоят марки этого реестра.
2. Столбец «Колер. карта» — позиции колерной карты (лист 42): К — окраска по коду цвета, КМ — материал без кода цвета; «Помещения» — номера по экспликации; количества — по ведомости отделки помещений (лист 40).
3. Марки позиций: один префикс — один вид позиций на весь альбом (двери Д, окна ОК, мебель М, сантехприборы П, декор ДК, текстиль Т, колерная карта К и КМ, радиаторы РО, розетки Р, выключатели S, светильники Св; стояки — «Ст» и система, например «Ст К1-1»). Совпадение префиксов у разных видов — замечание к исходным данным, при выпуске исправляется в модели.

Допущения и предложения на листе

Основа листа: размеры сняты со скана обмерного плана KV design (см): часть подписей не читается, помещения выровнены по читаемым размерам; контрольный обмер не выполнен (К-1); высота потолка 2650 мм принята по отметкам обмера (Н = 2,50…2,66 м, ригель 2,28 м) — уточнить при обмере (К-2); толщины стен 300 / 120 мм приняты, межквартирная стена и колонны — по скану, не замерены (К-1); разрешённая мощность 15 кВт принята по типовым ТУ; при объединении двух квартир — переоформление ТУ (К-4).

Знак «**» — предложение проектировщика, заказчиком не утверждено (согласовать с заказчиком): записи в реестре нет: плинтус пом. 1–5, 7–10, акцент пом. 3, фартук пом. 5 — артикул изделия не выбран: позиция описана характеристиками («аналог по характеристикам»), артикул выбирается при закупке.

См. лист открытых вопросов (лист 6, записи К-1, К-2, К-4).

Изм.	Кол.уч	Лист	№ док.	Подп.	Дата
Разраб.		Кырлан А.С.			18.10.26
Пров.					
ГИП					
Н. контр.					
Утв.					

ГД-2026-009-АИ

Квартира 103 м²

Общая площадь 100,72* м² · * размеры со скана, не замерены (реестр — л. 6, К-1)

Дизайн-проект интерьера

Стадия	Лист	Листов
РП	64	96

Реестр марок отделки и позиций альбома (продолжение)

М б/м

Кырлан Александр Сергеевич

выпуск 18.10.2026 № 53dc234b8d · стр. 75 из 135

Схема расположения развёрток и узлов

План квартиры: марки развёрток по помещениям, выноски узлов, ведомость «марка → лист»

ПРЕДВАРИТЕЛЬНО · не для производства работ · открыто пунктов: 4 (реестр — л. 6)

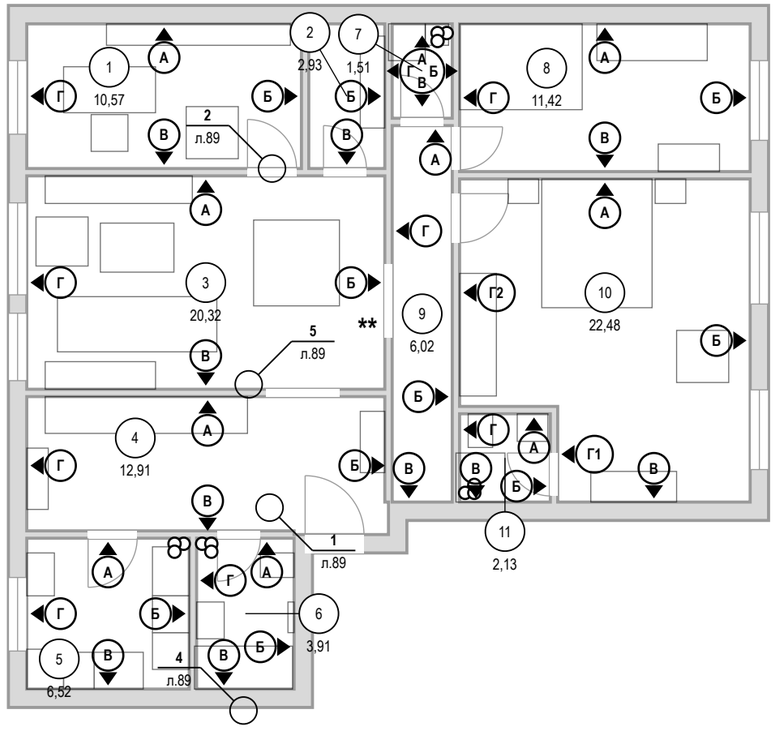

Развёртки и узлы: марка → лист

Марка	Помещение / узел	Лист
А, Б	Кабинет-библиотека (пом. 1)	66
В, Г	Кабинет-библиотека (пом. 1)	67
Б, В	Кладовая (пом. 2)	68
А, Б	Гостиная-столовая (пом. 3)	69
В, Г	Гостиная-столовая (пом. 3)	70
А, Б	Прихожая-холл (пом. 4)	71
В, Г	Прихожая-холл (пом. 4)	72
А	Кухня (пом. 5)	73
Б	Кухня (пом. 5)	74
В	Кухня (пом. 5)	75
Г	Кухня (пом. 5)	76
А, Б	Ванная (пом. 6)	77
В	Ванная (пом. 6)	78
Г	Ванная (пом. 6)	79
А, Б, В, Г	Постирочная (пом. 7)	80
А, Б	Спальня 2 (пом. 8)	81
В, Г	Спальня 2 (пом. 8)	82
А, Б, В	Коридор (пом. 9)	83
Г	Коридор (пом. 9)	84
А, Б	Спальня мастер (пом. 10)	85
В, Г1, Г2	Спальня мастер (пом. 10)	86
А, Б	Ванная мастер (пом. 11)	87
В, Г	Ванная мастер (пом. 11)	88
узел 1	Порог 15 мм: мокрая зона — жилое помещение	89
узел 2	Дверь скрытого монтажа в плоскости стены, плинтус	89
узел 3	Короб стояков К1-1, К1-2 (кухня) с люком и звукоизоляцией	89
узел 4	Гидроизоляция санузла: заход на стены 200 мм, примыкание ванны	89
узел 5	Плинтус МДФ 80×16 мм у окрашенной стены	89

Допущения и предложения на листе

Основа листа: размеры сняты со скана обмерного плана KV design (см): часть подписей не читается, помещения выровнены по читаемым размерам; контрольный обмер не выполнен (К-1); высота потолка 2650 мм принята по отметкам обмера (Н = 2,50…2,66 м, ригель 2,28 м) — уточнить при обмере (К-2); толщины стен 300 / 120 мм приняты, межквартирная стена и колонны — по скану, не замерены (К-1); разрешённая мощность 15 кВт принята по типовым ТУ; при объединении двух квартир — переоформление ТУ (К-4).

Знак «**» — предложение проектировщика, заказчиком не утверждено (согласовать с заказчиком): К-5: дверь пом. 3 (стена Б) — проём в межквартирной стене — объединение квартир, предложение до техзаключения.

См. лист открытых вопросов (лист 6, записи К-1, К-2, К-4, К-5).

Условные обозначения

- (А) ▼ — марка развёртки: буква стены, стрелка — взгляд
- ○ — выноска узла: над полкой — узел, под полкой — лист
- (1) — номер помещения, площадь м²

1000 мм · печать 1:1

Примечания

1. Развёртки — вид на стену изнутри помещения; буквы стен — одна система на весь альбом (как на листах выводов, плитки и отделки).
2. Стены без электроточек, мебели, декора и акцентной отделки развёрток не имеют: их отделка — по ведомости отделки помещений.
3. Узлы — на листе узлов; места применения — по выноскам этого листа и ведомости «марка → лист».

Изм.	Кол.уч	Лист	№ док.	Подп.	Дата
Разраб.		Кырлан А.С.			18.10.26
Пров.					
ГИП					
Н. контр.					
Утв.					

ГД-2026-009-АИ

Квартира 103 м²

Общая площадь 100,72* м² · * размеры со скана, не замерены (реестр — л. 6, К-1)

Дизайн-проект интерьера

Стадия	Лист	Листов
РП	65	96

Схема расположения развёрток и узлов

М 1:100

Кырлан Александр Сергеевич

выпуск 18.10.2026 № 53dc234b8d · стр. 76 из 135

Развёртки стен А, Б. Кабинет-библиотека (пом. 1)

Кабинет-библиотека (пом. 1) · вид изнутри помещения · размеры в мм, отметки в м

ПРЕДВАРИТЕЛЬНО · не для производства работ · открыто пунктов: 4 (реестр — л. 6)

Развёртка стены А

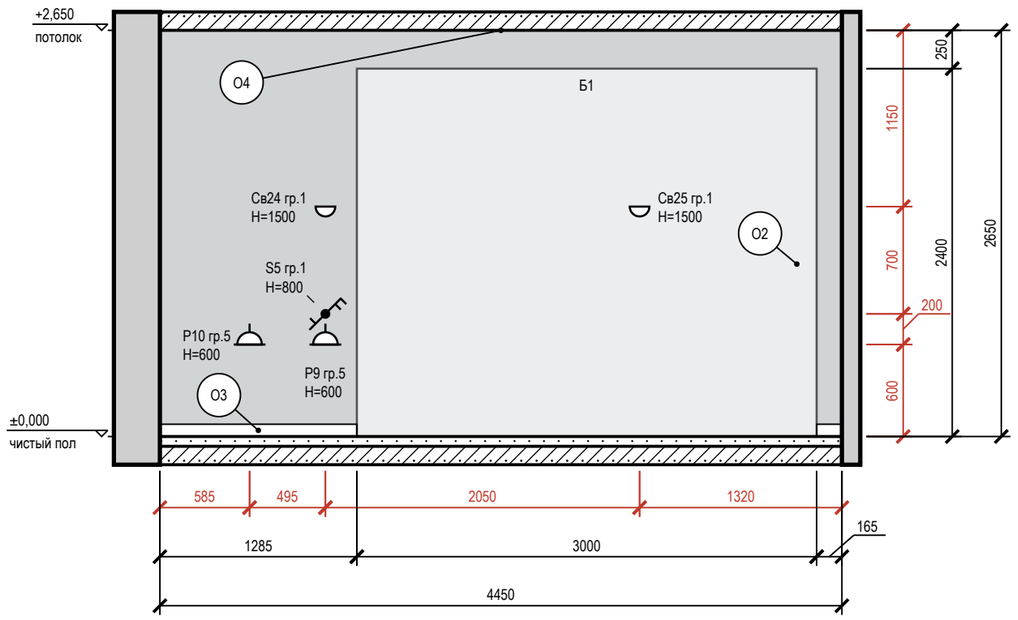

Развёртка стены Б

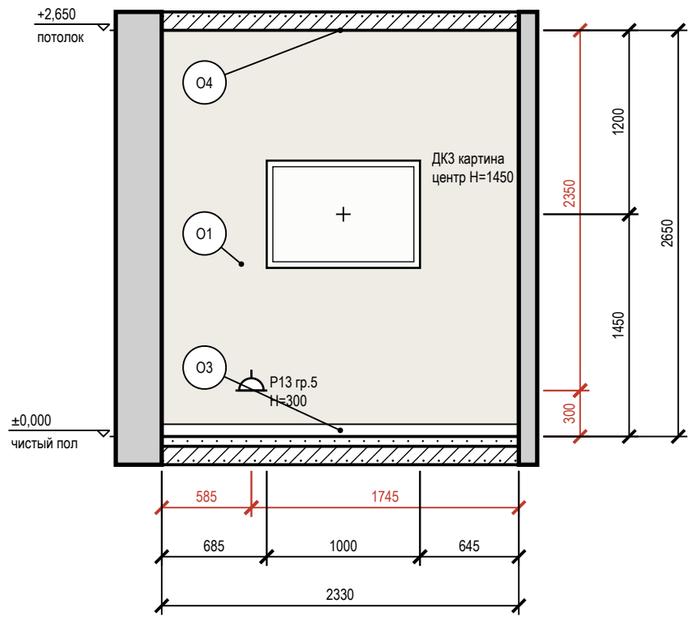

Условные обозначения

- розетка с заземляющим контактом; у знака — марка, ×N постов в рамке, гр. — группа щита, H — высота оси, мм
- выключатель одноклавишный
- выключатель двухклавишный (флажков — по числу клавиш)
- выключатель с проходной или перекрёстной клавишей (обратный флажок); тип клавиши — в подписи
- светильник настенный (бра), H — высота оси
- привязки точек и выводов от угла и от пола, мм
- мебель и приборы — фасад по расстановке (условно)
- картина (декор): марка Д, крест — центр, H — высота центра, мм
- стены и перекрытия в сечении
- окраска: тон — цвет по коду производителя (условно)
- О1 — марка отделки по реестру отделки альбома
- А — марка развёртки: буква стены, стрелка — взгляд

Схема развёрток (М 1:100)

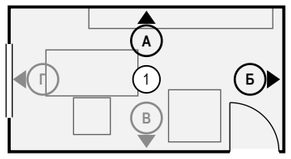

Ведомость отделки (на листе)

Марка	Поверхность	Материал, изделие	Цвет, код	Кол.
О1	стены	окраска, Farrow & Ball Modern Emulsion, матовая, подготовка Q3	Farrow & Ball No. 291 «School House White тёплый меловой белый»	6,2 м²
О2	акцентная стена	окраска, Farrow & Ball Modern Emulsion, матовая, подготовка Q3	Farrow & Ball No. 289 «Inchyra Blue — тёмный сине-серый»	11,8 м²
О3	плинтус	плинтус МДФ, h 80 мм, аналог: плинтус МДФ под покраску 80×16	Farrow & Ball No. 291 «School House White тёплый меловой белый»	3,8 м
О4	потолок	окраска, Tikkurila Anti-Reflex 2, глубокоматовая, подготовка Q3	NCS S 0502-Y «Белый с лёгкой желтизной»	10,6 м²

Допущения и предложения на листе

Основа листа: размеры сняты со скана обмерного плана KV design (см): часть подписей не читается, помещения выровнены по читаемым размерам; контрольный обмер не выполнен (К-1); высота потолка 2650 мм принята по отметкам обмера (H = 2,50…2,66 м, ригель 2,28 м) — уточнить при обмере (К-2); толщины стен 300 / 120 мм приняты, межквартирная стена и колонны — по скану, не замерены (К-1); разрешённая мощность 15 кВт принята по типовым ТУ; при объединении двух квартир — переоформление ТУ (К-4).
См. лист открытых вопросов (лист 6, записи К-1, К-2, К-4).

Примечания

1. Развёртки — вид на стену изнутри помещения, по часовой стрелке; расположение — на схеме листа и на листе 65; размеры — в мм по чистовым поверхностям; отметки — в м от ±0,000; высоты H — от чистого пола помещения до оси изделия, у декора — до центра.
2. Красные цепочки — привязки электроточек и выводов: по горизонтали от угла чистовых стен, по вертикали от чистого пола, до оси изделия; звенья короче 3 мм на листе вынесены во второй ярус (ближняя к стене цепочка).
3. У знака электроточки: марка (Р — розетка, S — выключатель, Св — светильник, ЭВ — вывод кабеля), ×N — число постов в рамке, гр. — группа щита, H — высота оси от чистого пола, мм; группы по клавишам выключателя — на листе выключателей.
4. Схема мебели, приборов и декора не является технической документацией для производства мебели; габариты — по паспортам изделий.
5. Картины и зеркала крепить к основанию по паспорту изделия (закладные и анкеры — в перечне скрытых работ); крест — ось центра предмета.

1000 мм · печать 1:1

Изм.	Кол.уч	Лист	№ док.	Подп.	Дата
Разраб.		Кырлан А.С.			18.10.26
Пров.					
ГИП					
Н. контр.					
Утв.					

ГД-2026-009-АИ

Квартира 103 м²

Общая площадь 100,72* м² · * размеры со скана, не замерены (реестр — л. 6, К-1)

Дизайн-проект интерьера

Стадия	Лист	Листов
РП	66	96

Развёртки стен А, Б. Кабинет-библиотека (пом. 1)

М 1:40

Кырлан Александр Сергеевич

выпуск 18.10.2026 № 53dc234b8d · стр. 77 из 135

Развёртки стен В, Г. Кабинет-библиотека (пом. 1)

Кабинет-библиотека (пом. 1) · вид изнутри помещения · размеры в мм, отметки в м

ПРЕДВАРИТЕЛЬНО · не для производства работ · открыто пунктов: 4 (реестр — л. 6)

Развёртка стены В

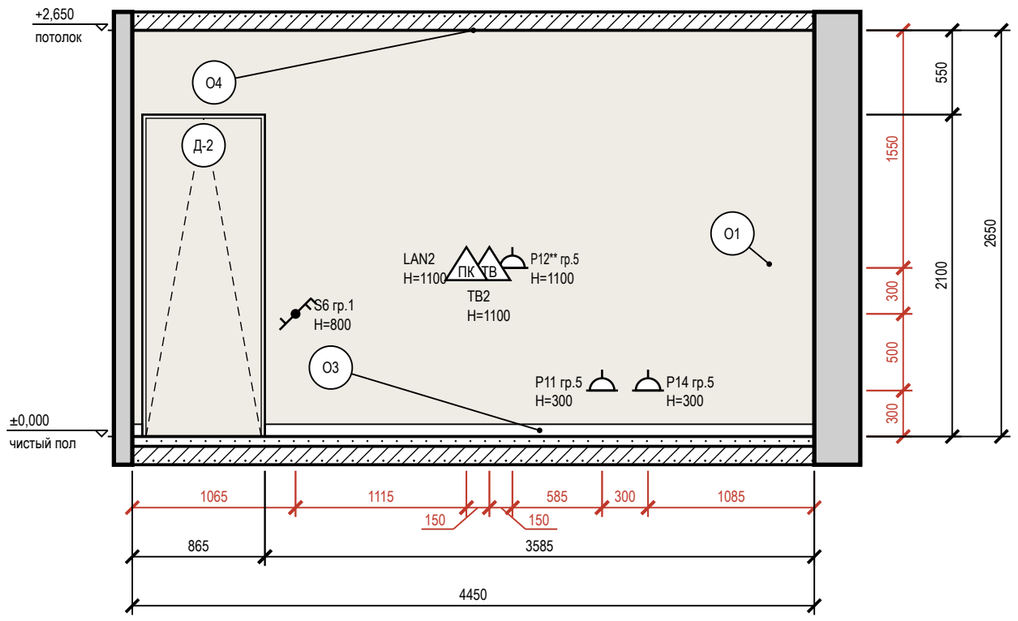

Развёртка стены Г

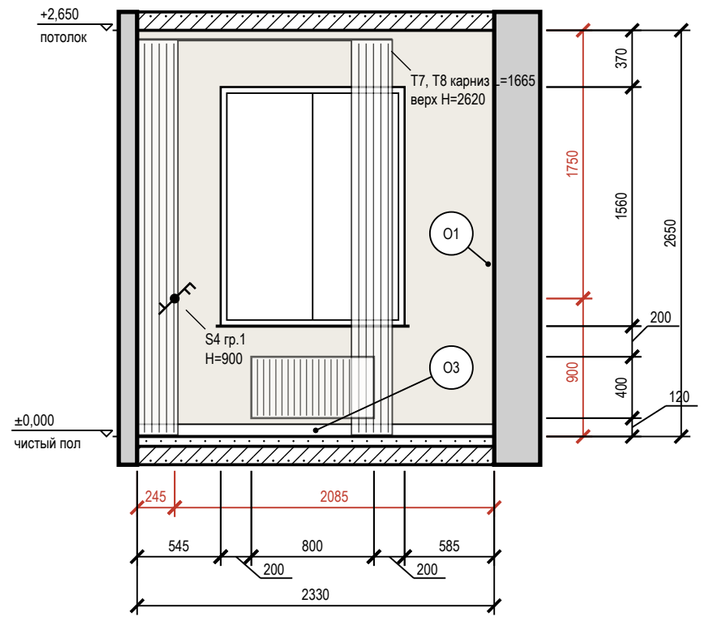

Условные обозначения

- розетка с заземляющим контактом; у знака — марка, ×N постов в рамке, гр. — группа щита, H — высота оси, мм
- выключатель одноклавишный
- выключатель двухклавишный (флажков — по числу клавиш)
- выключатель с проходной или перекрёстной клавишей (обратный флажок); тип клавиши — в подписи
- ПК — розетка компьютерная RJ45
- ТВ — розетка телевизионная
- привязки точек и выводов от угла и от пола, мм
- мебель и приборы — фасад по расстановке (условно)
- карниз (шина) и шторы в собранном виде: марка Т, длина L, верх H
- дверь скрытого монтажа: полотно в плоскости стены (узел — на листе узлов)
- окно: проём, рама, подоконник
- радиатор отопления; марка — по плану отопления
- стены и перекрытия в сечении
- окраска: тон — цвет по коду производителя (условно)
- О1 — марка отделки по реестру отделки альбома
- А — марка развёртки: буква стены, стрелка — взгляд

Схема развёрток (М 1:100)

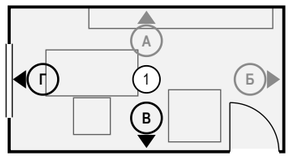

Ведомость отделки (на листе)

Марка	Поверхность	Материал, изделие	Цвет, код	Кол.
О1	стены	окраска, Farrow & Ball Modern Emulsion, матовая, подготовка Q3	Farrow & Ball No. 291 «School House White тёплый меловой белый»	14,4 м²
О3	плинтус	плинтус МДФ, h 80 мм, аналог: плинтус МДФ под покраску 80×16	Farrow & Ball No. 291 «School House White тёплый меловой белый»	6 м
О4	потолок	окраска, Tikkurila Anti-Reflex 2, глубокоматовая, подготовка Q3	NCS S 0502-Y «Белый с лёгкой желтизной»	10,6 м²

Допущения и предложения на листе

Основа листа: размеры сняты со скана обмерного плана KV design (см): часть подписей не читается, помещения выровнены по читаемым размерам; контрольный обмер не выполнен (К-1); высота потолка 2650 мм принята по отметкам обмера (H = 2,50…2,66 м, ригель 2,28 м) — уточнить при обмере (К-2); толщины стен 300 / 120 мм приняты, межквартирная стена и колонны — по скану, не замерены (К-1); разрешённая мощность 15 кВт принята по типовым ТУ; при объединении двух квартир — переоформление ТУ (К-4).

Знак «**» — предложение проектировщика, заказчиком не утверждено (согласовать с заказчиком): записи в реестре нет: Р12 — высота 1100 мм выше нормы 1 м (ПУЭ 6.6.30) по назначению: питание ТВ над комодом, в одной зоне с выводами ТВ2 и LAN2.

См. лист открытых вопросов (лист 6, записи К-1, К-2, К-4).

Примечания

1. Развёртки — вид на стену изнутри помещения, по часовой стрелке; расположение — на схеме листа и на листе 65; размеры — в мм по чистовым поверхностям; отметки — в м от ±0,000; высоты H — от чистого пола помещения до оси изделия, у декора — до центра.
2. Красные цепочки — привязки электроточек и выводов: по горизонтали от угла чистовых стен, по вертикали от чистого пола, до оси изделия; звенья короче 3 мм на листе вынесены во второй ярус (ближняя к стене цепочка).
3. У знака электроточки: марка (Р — розетка, S — выключатель, Св — светильник, ЭВ — вывод кабеля), ×N — число постов в рамке, гр. — группа щита, H — высота оси от чистого пола, мм; группы по клавишам выключателя — на листе выключателей.
4. Схема мебели, приборов и декора не является технической документацией для производства мебели; габариты — по паспортам изделий.
5. Карнизы (шины) — по ведомости текстиля декоратора; длина L и верх H — по развёртке, крепление — до окраски потолка.
6. Двери скрытого монтажа — полотно в плоскости стены, отделка стены по полотну, плинтус прерывается у короба (узел — на листе узлов).
7. Линии узора (швы плитки, складки штор, рёбра радиаторов) прерываются у знаков и выносок — просвет между линиями не менее 0,7 мм.

1000 мм · печать 1:1

						ГД-2026-009-АИ
						Квартира 103 м²
Изм.	Кол.уч	Лист	№ док.	Подп.	Дата	Общая площадь 100,72* м² · * размеры со скана, не замерены (реестр — л. 6, К-1)
Разраб.		Кырлан А.С.			18.10.26	Дизайн-проект интерьера
Пров.						Стадия: РП · Лист: 67 · Листов: 96
ГИП						
Н. контр.						**Развёртки стен В, Г. Кабинет-библиотека (пом. 1)** · М 1:40
Утв.						**Кырлан Александр Сергеевич**

выпуск 18.10.2026 № 53dc234b8d · стр. 78 из 135

Развёртки стен. Кладовая (пом. 2)

Кладовая (пом. 2) · вид изнутри помещения · размеры в мм, отметки в м

ПРЕДВАРИТЕЛЬНО · не для производства работ · открыто пунктов: 4 (реестр — л. 6)

Развёртка стены Б

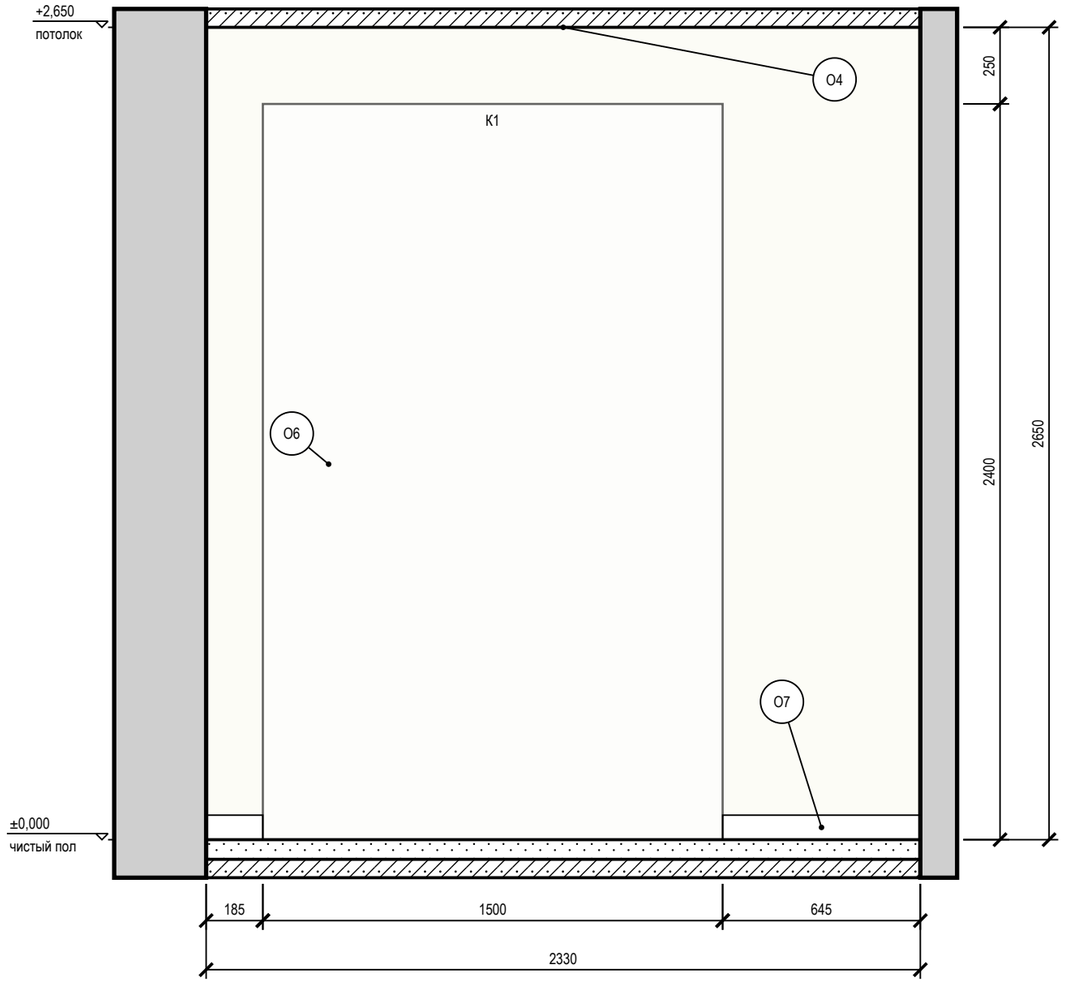

Развёртка стены В

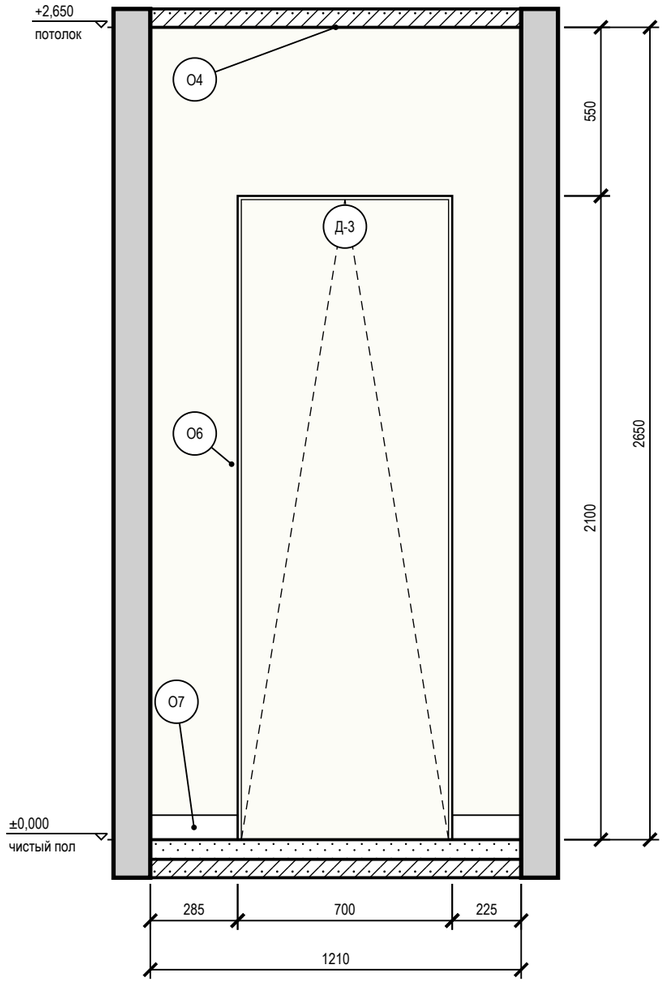

Схема развёрток (М 1:100)

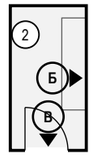

Условные обозначения

- привязки точек и выводов от угла и от пола, мм
- мебель и приборы — фасад по расстановке (условно)
- дверь скрытого монтажа: полотно в плоскости стены (узел — на листе узлов)
- стены и перекрытия в сечении
- окраска: тон — цвет по коду производителя (условно)
- О1 — марка отделки по реестру отделки альбома
- А — марка развёртки: буква стены, стрелка — взгляд

Допущения и предложения на листе

Основа листа: размеры сняты со скана обмерного плана KV design (см): часть подписей не читается, помещения выровнены по читаемым размерам; контрольный обмер не выполнен (К-1); высота потолка 2650 мм принята по отметкам обмера (Н = 2,50…2,66 м, ригель 2,28 м) — уточнить при обмере (К-2); толщины стен 300 / 120 мм приняты, межквартирная стена и колонны — по скану, не замерены (К-1); разрешённая мощность 15 кВт принята по типовым ТУ; при объединении двух квартир — переоформление ТУ (К-4).

См. лист открытых вопросов (лист 6, записи К-1, К-2, К-4).

Примечания

1. Развёртки — вид на стену изнутри помещения, по часовой стрелке; расположение — на схеме листа и на листе 65; размеры — в мм по чистовым поверхностям; отметки — в м от ±0,000; высоты Н — от чистого пола помещения до оси изделия, у декора — до центра.
2. Красные цепочки — привязки электроточек и выводов: по горизонтали от угла чистовых стен, по вертикали от чистого пола, до оси изделия; звенья короче 3 мм на листе вынесены во второй ярус (ближняя к стене цепочка).
3. У знака электроточки: марка (Р — розетка, S — выключатель, Св — светильник, ЭВ — вывод кабеля), ×N — число постов в рамке, гр. — группа щита, Н — высота оси от чистого пола, мм; группы по клавишам выключателя — на листе выключателей.
4. Схема мебели, приборов и декора не является технической документацией для производства мебели; габариты — по паспортам изделий.
5. Двери скрытого монтажа — полотно в плоскости стены, отделка стены по полотну, плинтус прерывается у короба (узел — на листе узлов).

1000 мм · печать 1:1

Изм.	Кол.уч	Лист	№ док.	Подп.	Дата
Разраб.		Кырлан А.С.			18.10.26
Пров.					
ГИП					
Н. контр.					
Утв.					

ГД-2026-009-АИ

Квартира 103 м²

Общая площадь 100,72* м² · * размеры со скана, не замерены (реестр — л. 6, К-1)

Дизайн-проект интерьера

Стадия	Лист	Листов
РП	68	96

Развёртки стен. Кладовая (пом. 2)

М 1:20

Кырлан Александр Сергеевич

выпуск 18.10.2026 № 53dc234b8d · стр. 79 из 135

Развёртки стен А, Б. Гостиная-столовая (пом. 3)

Гостиная-столовая (пом. 3) · вид изнутри помещения · размеры в мм, отметки в м

ПРЕДВАРИТЕЛЬНО · не для производства работ · открыто пунктов: 4 (реестр — л. 6)

Развёртка стены А

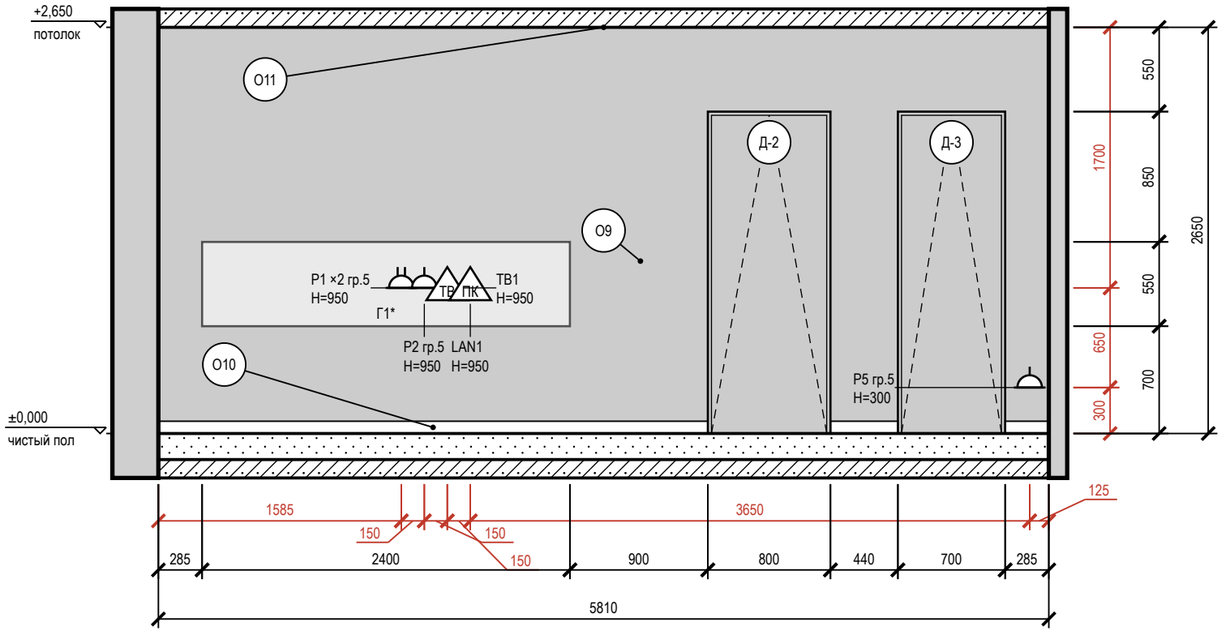

Развёртка стены Б

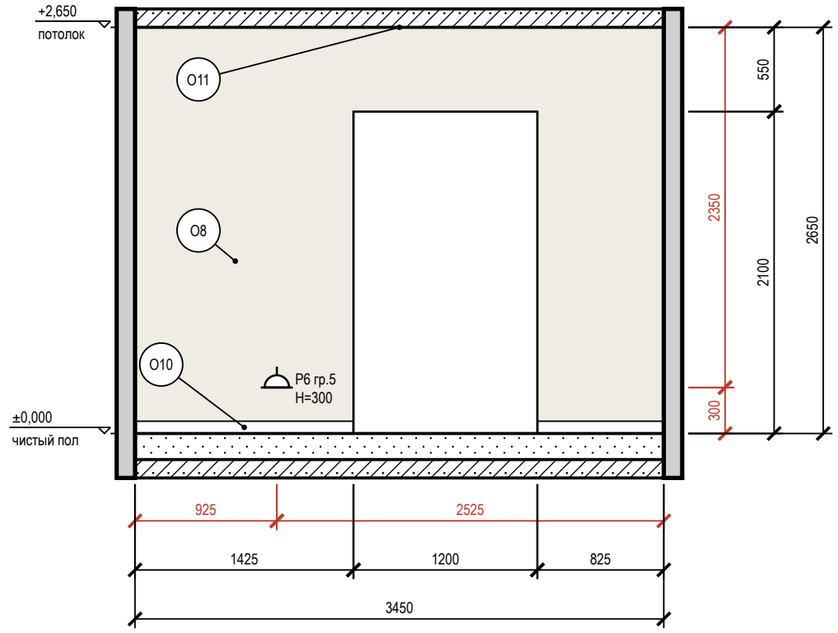

Схема развёрток (М 1:100)

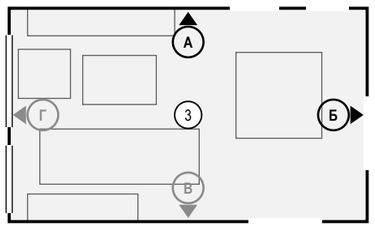

Условные обозначения

- розетка с заземляющим контактом; у знака — марка, ×N постов в рамке, гр. — группа щита, Н — высота оси, мм
- ПК / ТВ — розетка компьютерная RJ45 / розетка телевизионная
- привязки точек и выводов от угла и от пола, мм
- мебель и приборы — фасад по расстановке (условно)
- дверь скрытого монтажа: полотно в плоскости стены (узел — на листе узлов)
- дверной проём; марка двери — в кружке
- стены и перекрытия в сечении
- окраска: тон — цвет по коду производителя (условно)
- О1 — марка отделки по реестру отделки альбома
- А — марка развёртки: буква стены, стрелка — взгляд

Ведомость отделки (на листе)

Марка	Поверхность	Материал, изделие	Цвет, код	Кол.
О8	стены	окраска, Tikkurila Optiva 5 Matt, матовая, подготовка К3	Farrow & Ball No. 291 «School House White тёплый меловой белый»	6,6 м²
О9	акцентная стена	окраска, Tikkurila Optiva 5 Matt, аналог: интерьерная краска, класс 2 по EN 13300, глубокоматовая/матовая, база С, матовая, подготовка К3	Farrow & Ball No. 255 «Tanner's Brown — тёмный шоколад»	12,2 м²
О10	плинтус	плинтус МДФ, h 80 мм, аналог: плинтус МДФ под окраску 80×16 мм, полуглянцевая	Farrow & Ball No. 291 «School House White тёплый меловой белый»	6,6 м
О11	потолок	окраска, Tikkurila Anti-Reflex 2, глубокоматовая, подготовка Q3	Farrow & Ball No. 291 «School House White тёплый меловой белый»	20,3 м²

Допущения и предложения на листе

Основа листа: размеры сняты со скана обмерного плана KV design (см): часть подписей не читается, помещения выровнены по читаемым размерам; контрольный обмер не выполнен (К-1); высота потолка 2650 мм принята по отметкам обмера (Н = 2,50…2,66 м, ригель 2,28 м) — уточнить при обмере (К-2); толщины стен 300 / 120 мм приняты, межквартирная стена и колонны — по скану, не замерены (К-1); разрешённая мощность 15 кВт принята по типовым ТУ; при объединении двух квартир — переоформление ТУ (К-4).

Знак «**» — предложение проектировщика, заказчиком не утверждено (согласовать с заказчиком): К-5: дверь пом. 3 (стена Б) — проём в межквартирной стене — объединение квартир, предложение до техзаключения.

См. лист открытых вопросов (лист 6, записи К-1, К-2, К-4, К-5).

Примечания

1. Развёртки — вид на стену изнутри помещения, по часовой стрелке; расположение — на схеме листа и на листе 65; размеры — в мм по чистовым поверхностям; отметки — в м от ±0,000; высоты Н — от чистого пола помещения до оси изделия, у декора — до центра.
2. Красные цепочки — привязки электроточек и выводов: по горизонтали от угла чистовых стен, по вертикали от чистого пола, до оси изделия; звенья короче 3 мм на листе вынесены во второй ярус (ближняя к стене цепочка).
3. У знака электроточки: марка (Р — розетка, S — выключатель, Св — светильник, ЭВ — вывод кабеля), ×N — число постов в рамке, гр. — группа щита, Н — высота оси от чистого пола, мм; группы по клавишам выключателя — на листе выключателей.
4. Схема мебели, приборов и декора не является технической документацией для производства мебели; габариты — по паспортам изделий (* — высота не задана в проекте, показана по типовому изделию).
5. Двери скрытого монтажа — полотно в плоскости стены, отделка стены по полотну, плинтус прерывается у короба (узел — на листе узлов).

1000 мм · печать 1:1

Изм.	Кол.уч	Лист	№ док.	Подп.	Дата
Разраб.		Кырлан А.С.			18.10.26
Пров.					
ГИП					
Н. контр.					
Утв.					

ГД-2026-009-АИ

Квартира 103 м²

Общая площадь 100,72* м² · * размеры со скана, не замерены (реестр — л. 6, К-1)

Дизайн-проект интерьера

Стадия	Лист	Листов
РП	69	96

Развёртки стен А, Б. Гостиная-столовая (пом. 3)

М 1:40

Кырлан Александр Сергеевич

выпуск 18.10.2026 № 53dc234b8d · стр. 80 из 135

Развёртки стен В, Г. Гостиная-столовая (пом. 3)

Гостиная-столовая (пом. 3) · вид изнутри помещения · размеры в мм, отметки в м

ПРЕДВАРИТЕЛЬНО · не для производства работ · открыто пунктов: 4 (реестр — л. 6)

Развёртка стены В

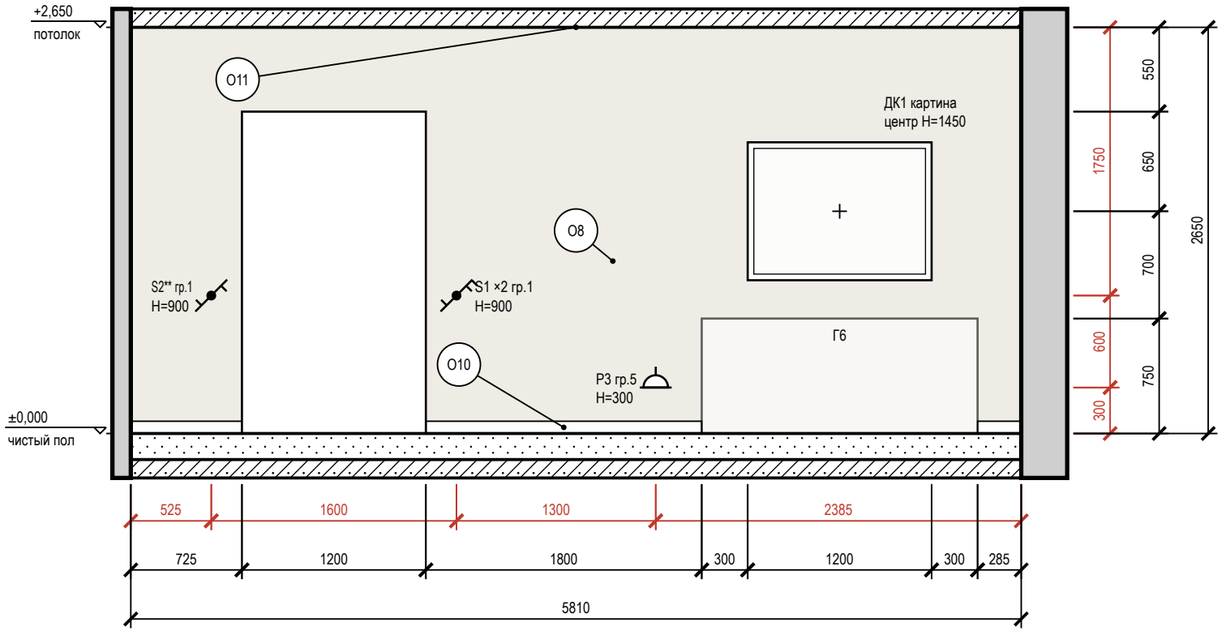

Развёртка стены Г

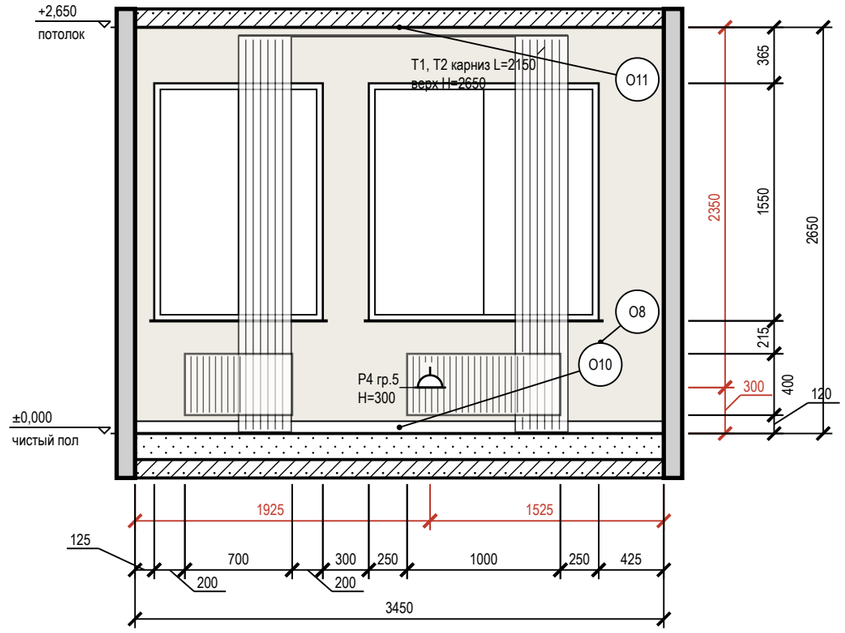

Схема развёрток (М 1:100)

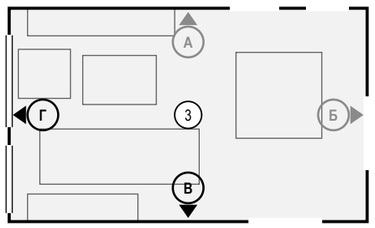

Условные обозначения

- розетка с заземляющим контактом; у знака — марка, ×N постов в рамке, гр. — группа щита, Н — высота оси, мм
- выключатель одноклавишный
- выключатель двухклавишный (флажков — по числу клавиш)
- выключатель с проходной или перекрёстной клавишей (обратный флажок); тип клавиши — в подписи
- привязки точек и выводов от угла и от пола, мм
- мебель и приборы — фасад по расстановке (условно)
- картина (декор): марка Д, крест — центр, Н — высота центра, мм
- карниз (шина) и шторы в собранном виде: марка Т, длина L, верх Н
- окно: проём, рама, подоконник
- дверной проём; марка двери — в кружке
- радиатор отопления; марка — по плану отопления
- стены и перекрытия в сечении
- окраска: тон — цвет по коду производителя (условно)
- О1 — марка отделки по реестру отделки альбома
- А — марка развёртки: буква стены, стрелка — взгляд

Ведомость отделки (на листе)

Марка	Поверхность	Материал, изделие	Цвет, код	Кол.
О8	стены	окраска, Tikkurila Optiva 5 Matt, матовая, подготовка К3	Farrow & Ball No. 291 «School House White — тёплый меловой белый»	18 м²
О10	плинтус	плинтус МДФ, h 80 мм, аналог: плинтус МДФ под окраску 80×16 мм, полуглянцевая	Farrow & Ball No. 291 «School House White — тёплый меловой белый»	6,3 м
О11	потолок	окраска, Tikkurila Anti-Reflex 2, глубокоматовая, подготовка Q3	Farrow & Ball No. 291 «School House White — тёплый меловой белый»	20,3 м²

Допущения и предложения на листе

Основа листа: размеры сняты со скана обмерного плана KV design (см): часть подписей не читается, помещения выровнены по читаемым размерам; контрольный обмер не выполнен (К-1); высота потолка 2650 мм принята по отметкам обмера (Н = 2,50…2,66 м, ригель 2,28 м) — уточнить при обмере (К-2); толщины стен 300 / 120 мм приняты, межквартирная стена и колонны — по скану, не замерены (К-1); разрешённая мощность 15 кВт принята по типовым ТУ; при объединении двух квартир — переоформление ТУ (К-4).

Знак «**» — предложение проектировщика, заказчиком не утверждено (согласовать с заказчиком): К-5: дверь пом. 3 (стена Б) — проём в межквартирной стене — объединение квартир, предложение до техзаключения; записи в реестре нет: S2 — светорегулятор добавлен под диммируемую ленту L3; уровни сценариев выбраны конвейером.

См. лист открытых вопросов (лист 6, записи К-1, К-2, К-4, К-5).

Примечания

1. Развёртки — вид на стену изнутри помещения, по часовой стрелке; расположение — на схеме листа и на листе 65; размеры — в мм по чистовым поверхностям; отметки — в м от ±0,000; высоты Н — от чистого пола помещения до оси изделия, у декора — до центра.
2. Красные цепочки — привязки электроточек и выводов: по горизонтали от угла чистовых стен, по вертикали от чистого пола, до оси изделия; звенья короче 3 мм на листе вынесены во второй ярус (ближняя к стене цепочка).
3. У знака электроточки: марка (Р — розетка, S — выключатель, Св — светильник, ЭВ — вывод кабеля), ×N — число постов в рамке, гр. — группа щита, Н — высота оси от чистого пола, мм; группы по клавишам выключателя — на листе выключателей.
4. Схема мебели, приборов и декора не является технической документацией для производства мебели; габариты — по паспортам изделий.
5. Картины и зеркала крепить к основанию по паспорту изделия (закладные и анкеры — в перечне скрытых работ); крест — ось центра предмета.
6. Карнизы (шины) — по ведомости текстиля декоратора; длина L и верх Н — по развёртке, крепление — до окраски потолка.
7. Линии узора (швы плитки, складки штор, рёбра радиаторов) прерываются у знаков и выносок — просвет между линиями не менее 0,7 мм.

1000 мм · печать 1:1

Изм.	Кол.уч	Лист	№ док.	Подп.	Дата
Разраб.		Кырлан А.С.			18.10.26
Пров.					
ГИП					
Н. контр.					
Утв.					

ГД-2026-009-АИ

Квартира 103 м²

Общая площадь 100,72* м² · * размеры со скана, не замерены (реестр — л. 6, К-1)

Дизайн-проект интерьера

Стадия	Лист	Листов
РП	70	96

Развёртки стен В, Г. Гостиная-столовая (пом. 3)

М 1:40

Кырлан Александр Сергеевич

выпуск 18.10.2026 № 53dc234b8d · стр. 81 из 135

Развёртки стен А, Б. Прихожая-холл (пом. 4)

Прихожая-холл (пом. 4) · вид изнутри помещения · размеры в мм, отметки в м

ПРЕДВАРИТЕЛЬНО · не для производства работ · открыто пунктов: 4 (реестр — л. 6)

Развёртка стены А

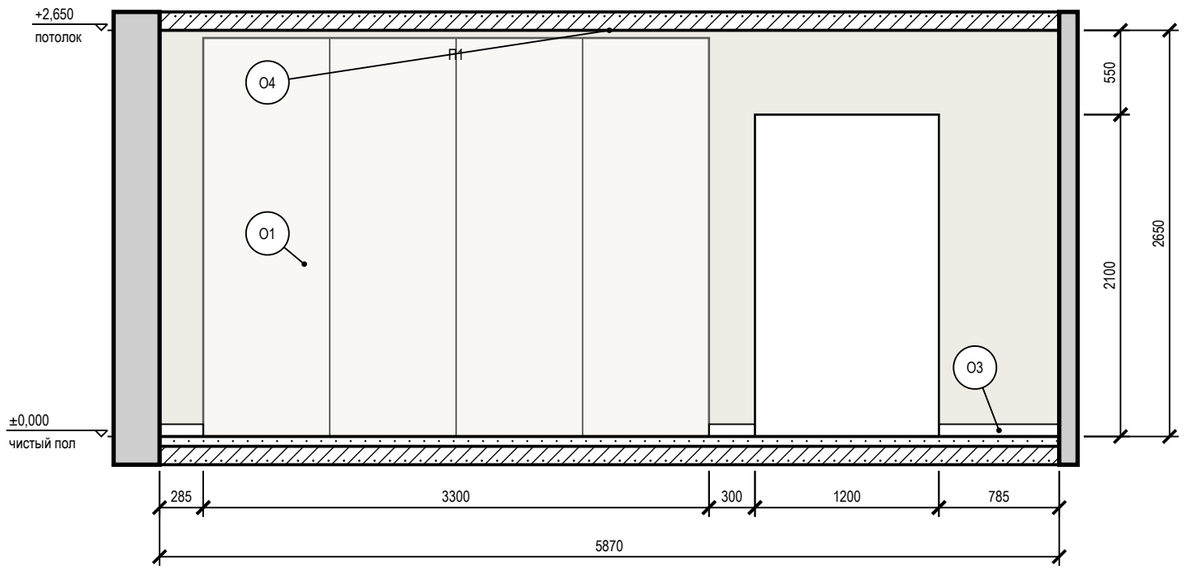

Развёртка стены Б

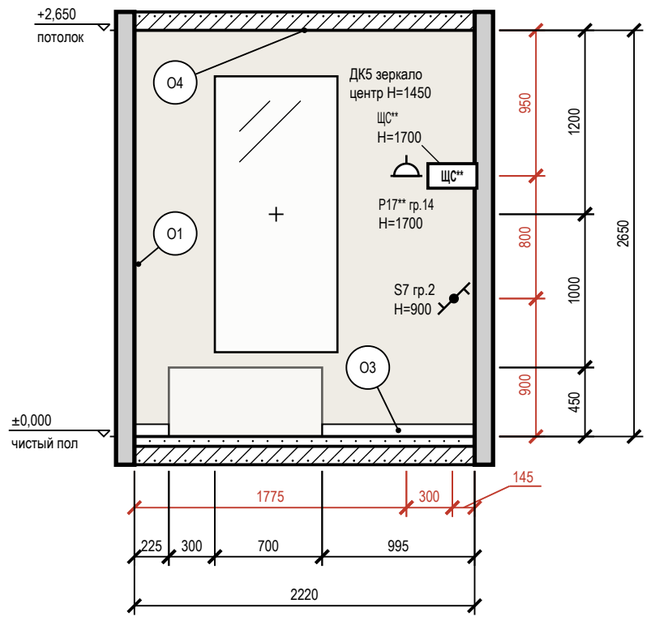

Схема развёрток (М 1:100)

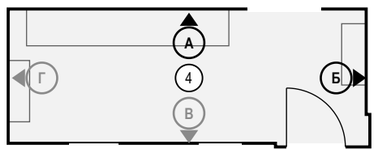

Условные обозначения

- розетка с заземляющим контактом; у знака — марка, ×N постов в рамке, гр. — группа щита, Н — высота оси, мм
- выключатель одноклавишный
- выключатель с проходной или перекрёстной клавишей (обратный флажок); тип клавиши — в подписи
- ЩК — щит квартирный
- привязки точек и выводов от угла и от пола, мм
- мебель и приборы — фасад по расстановке (условно)
- зеркало: марка Д, крест — центр, Н — высота центра, мм
- дверной проём; марка двери — в кружке
- стены и перекрытия в сечении
- окраска: тон — цвет по коду производителя (условно)
- О1 — марка отделки по реестру отделки альбома
- А — марка развёртки: буква стены, стрелка — взгляд

Ведомость отделки (на листе)

Марка	Поверхность	Материал, изделие	Цвет, код	Кол.
О1	стены	окраска, Farrow & Ball Modern Emulsion, матовая, подготовка Q3	Farrow & Ball No. 291 «School House White тёплый меловой белый»	18,9 м²
О3	плинтус	плинтус МДФ, h 80 мм, аналог: плинтус МДФ под покраску 80×16	Farrow & Ball No. 291 «School House White тёплый меловой белый»	2,6 м
О4	потолок	окраска, Tikkurila Anti-Reflex 2, глубокоматовая, подготовка Q3	NCS S 0502-Y «Белый с лёгкой желтизной»	12,9 м²

Допущения и предложения на листе

Основа листа: размеры сняты со скана обмерного плана KV design (см): часть подписей не читается, помещения выровнены по читаемым размерам; контрольный обмер не выполнен (К-1); высота потолка 2650 мм принята по отметкам обмера (Н = 2,50…2,66 м, ригель 2,28 м) — уточнить при обмере (К-2); толщины стен 300 / 120 мм приняты, межквартирная стена и колонны — по скану, не замерены (К-1); разрешённая мощность 15 кВт принята по типовым ТУ; при объединении двух квартир — переоформление ТУ (К-4).

Знак «**» — предложение проектировщика, заказчиком не утверждено (согласовать с заказчиком): записи в реестре нет: Р17 — высота 1700 мм выше нормы 1 м (ПУЭ 6.6.30) по назначению: питание слаботочного щита ЩС, рядом со щитом на его высоте; ЩС — щит слаботочный: место и состав.

См. лист открытых вопросов (лист 6, записи К-1, К-2, К-4).

Примечания

1. Развёртки — вид на стену изнутри помещения, по часовой стрелке; расположение — на схеме листа и на листе 65; размеры — в мм по чистовым поверхностям; отметки — в м от ±0,000; высоты Н — от чистого пола помещения до оси изделия, у декора — до центра.
2. Красные цепочки — привязки электроточек и выводов: по горизонтали от угла чистовых стен, по вертикали от чистого пола, до оси изделия; звенья короче 3 мм на листе вынесены во второй ярус (ближняя к стене цепочка).
3. У знака электроточки: марка (Р — розетка, S — выключатель, Св — светильник, ЭВ — вывод кабеля), ×N — число постов в рамке, гр. — группа щита, Н — высота оси от чистого пола, мм; группы по клавишам выключателя — на листе выключателей.
4. Схема мебели, приборов и декора не является технической документацией для производства мебели; габариты — по паспортам изделий.
5. Картины и зеркала крепить к основанию по паспорту изделия (закладные и анкеры — в перечне скрытых работ); крест — ось центра предмета.

1000 мм · печать 1:1

Изм.	Кол.уч	Лист	№ док.	Подп.	Дата
Разраб.		Кырлан А.С.			18.10.26
Пров.					
ГИП					
Н. контр.					
Утв.					

ГД-2026-009-АИ

Квартира 103 м²

Общая площадь 100,72* м² · * размеры со скана, не замерены (реестр — л. 6, К-1)

Дизайн-проект интерьера

Стадия	Лист	Листов
РП	71	96

Развёртки стен А, Б. Прихожая-холл (пом. 4)

М 1:40

Кырлан Александр Сергеевич

выпуск 18.10.2026 № 53dc2348d8d · стр. 82 из 135

Развёртки стен В, Г. Прихожая-холл (пом. 4)

Прихожая-холл (пом. 4) · вид изнутри помещения · размеры в мм, отметки в м

ПРЕДВАРИТЕЛЬНО · не для производства работ · открыто пунктов: 4 (реестр — л. 6)

Развёртка стены В

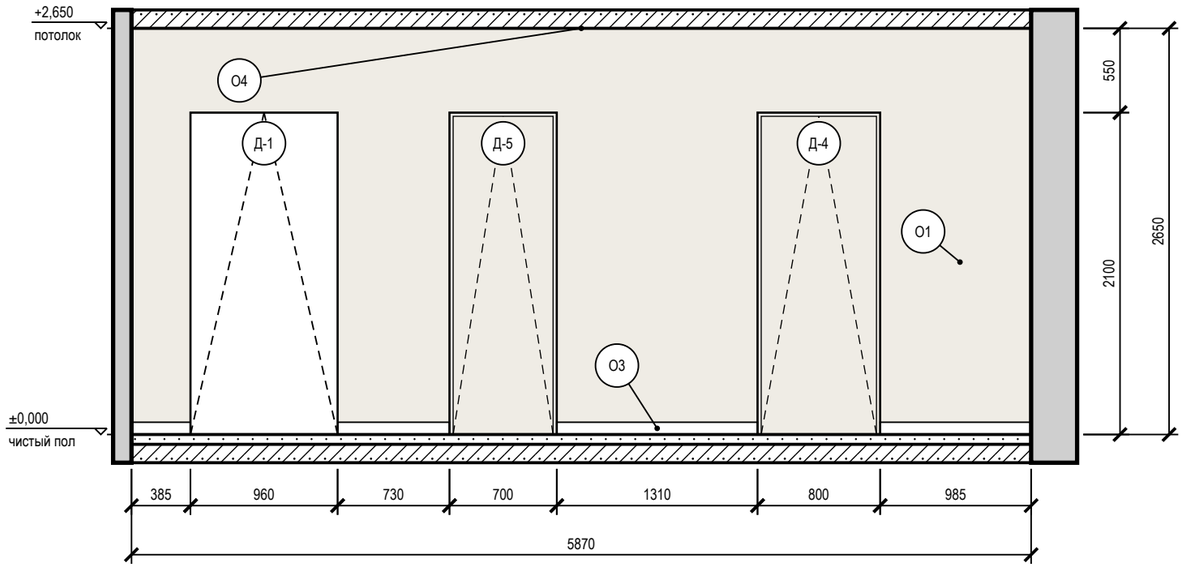

Развёртка стены Г

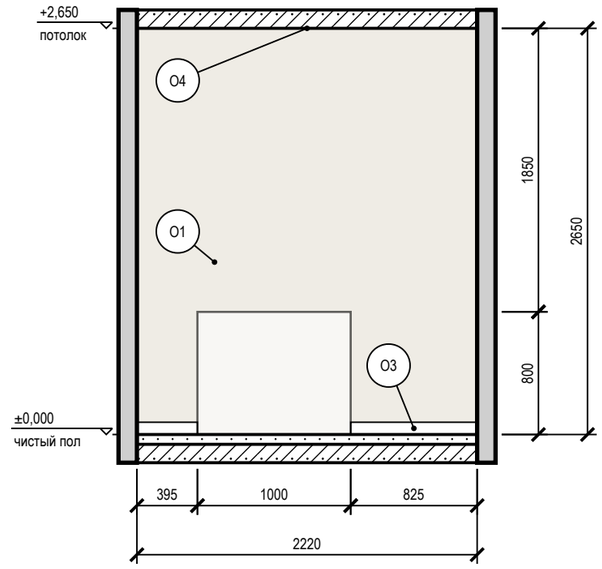

Схема развёрток (М 1:100)

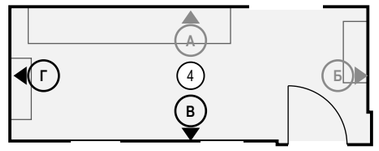

Условные обозначения

- привязки точек и выводов от угла и от пола, мм
- мебель и приборы — фасад по расстановке (условно)
- дверь скрытого монтажа: полотно в плоскости стены (узел — на листе узлов)
- дверной проём; марка двери — в кружке
- стены и перекрытия в сечении
- окраска: тон — цвет по коду производителя (условно)
- О1 — марка отделки по реестру отделки альбома
- А — марка развёртки: буква стены, стрелка — взгляд

Ведомость отделки (на листе)

Марка	Поверхность	Материал, изделие	Цвет, код	Кол.
О1	стены	окраска, Farrow & Ball Modern Emulsion, матовая, подготовка Q3	Farrow & Ball No. 291 «School House White тёплый меловой белый»	16,3 м²
О3	плинтус	плинтус МДФ, h 80 мм, аналог: плинтус МДФ под покраску 80×16	Farrow & Ball No. 291 «School House White тёплый меловой белый»	4,6 м
О4	потолок	окраска, Tikkurila Anti-Reflex 2, глубокоматовая, подготовка Q3	NCS S 0502-Y «Белый с лёгкой желтизной»	12,9 м²

Допущения и предложения на листе

Основа листа: размеры сняты со скана обмерного плана KV design (см): часть подписей не читается, помещения выровнены по читаемым размерам; контрольный обмер не выполнен (К-1); высота потолка 2650 мм принята по отметкам обмера (Н = 2,50…2,66 м, ригель 2,28 м) — уточнить при обмере (К-2); толщины стен 300 / 120 мм приняты, межквартирная стена и колонны — по скану, не замерены (К-1); разрешённая мощность 15 кВт принята по типовым ТУ; при объединении двух квартир — переоформление ТУ (К-4).
См. лист открытых вопросов (лист 6, записи К-1, К-2, К-4).

Примечания

1. Развёртки — вид на стену изнутри помещения, по часовой стрелке; расположение — на схеме листа и на листе 65; размеры — в мм по чистовым поверхностям; отметки — в м от ±0,000; высоты Н — от чистого пола помещения до оси изделия, у декора — до центра.
2. Красные цепочки — привязки электроточек и выводов: по горизонтали от угла чистовых стен, по вертикали от чистого пола, до оси изделия; звенья короче 3 мм на листе вынесены во второй ярус (ближняя к стене цепочка).
3. У знака электроточки: марка (Р — розетка, S — выключатель, Св — светильник, ЭВ — вывод кабеля), ×N — число постов в рамке, гр. — группа щита, Н — высота оси от чистого пола, мм; группы по клавишам выключателя — на листе выключателей.
4. Схема мебели, приборов и декора не является технической документацией для производства мебели; габариты — по паспортам изделий.
5. Двери скрытого монтажа — полотно в плоскости стены, отделка стены по полотну, плинтус прерывается у короба (узел — на листе узлов).

1000 мм · печать 1:1

Изм.	Кол.уч	Лист	№ док.	Подп.	Дата
Разраб.		Кырлан А.С.			18.10.26
Пров.					
ГИП					
Н. контр.					
Утв.					

ГД-2026-009-АИ

Квартира 103 м²

Общая площадь 100,72* м² · * размеры со скана, не замерены (реестр — л. 6, К-1)

Дизайн-проект интерьера

Стадия	Лист	Листов
РП	72	96

Развёртки стен В, Г. Прихожая-холл (пом. 4)

М 1:40

Кырлан Александр Сергеевич

выпуск 18.10.2026 № 53dc234b88d · стр. 83 из 135

Развёртка стены А. Кухня (пом. 5), кухонный фронт

Кухня (пом. 5) · вид изнутри помещения · размеры в мм, отметки в м

ПРЕДВАРИТЕЛЬНО · не для производства работ · открыто пунктов: 4 (реестр — л. 6)

Развёртка стены А

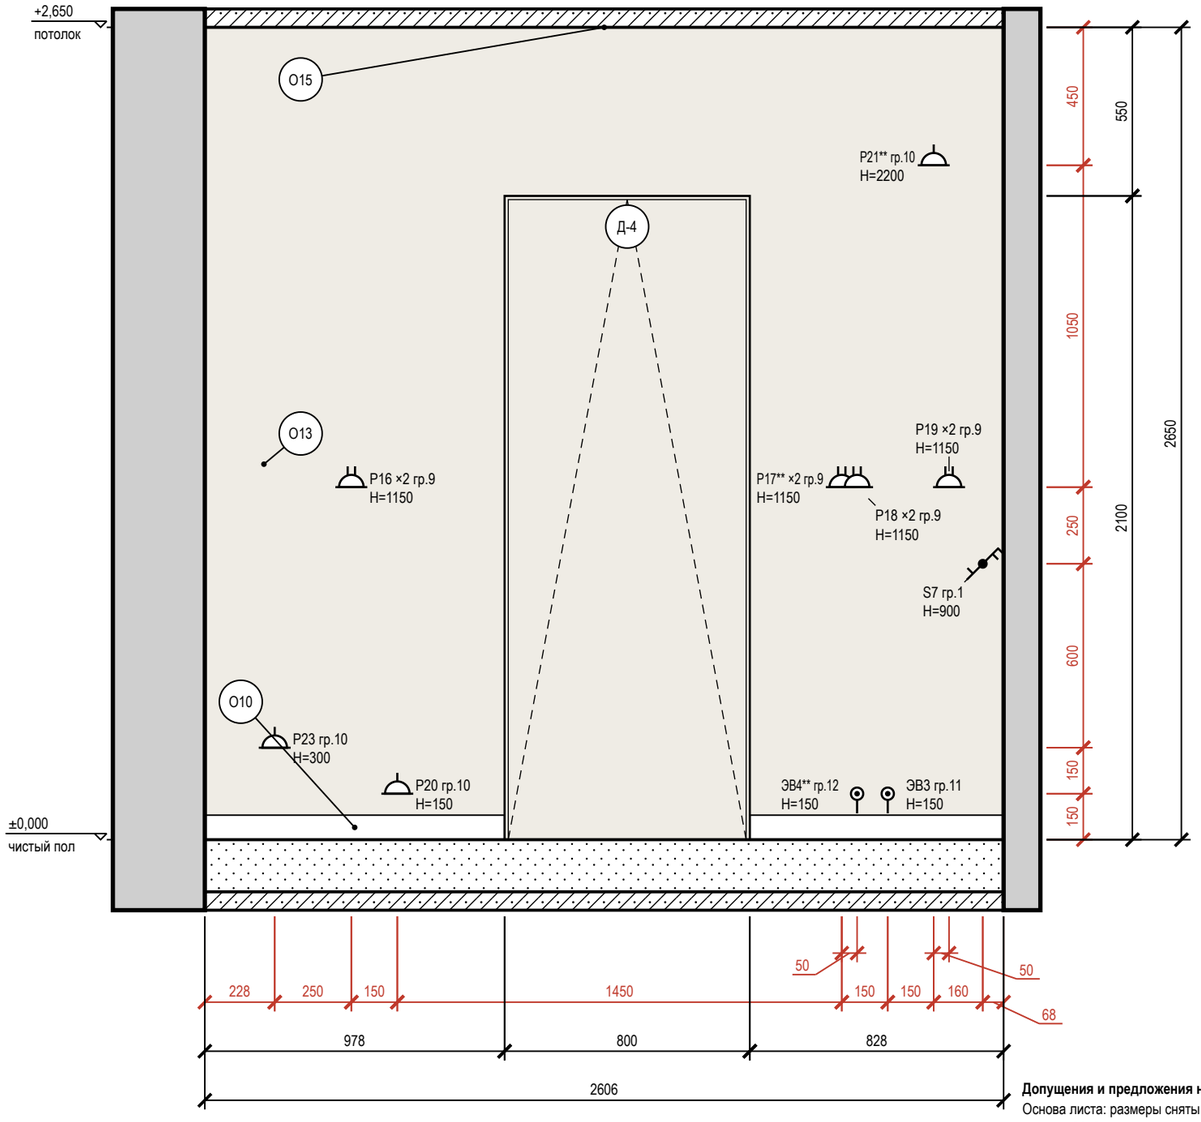

Схема развёрток (М 1:100)

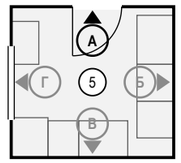

Условные обозначения

- розетка с заземляющим контактом; у знака — марка, ×N постов в рамке, гр. — группа щита, Н — высота оси, мм
- вывод кабеля для подключения прибора (без розетки), марка ЭВ
- выключатель одноклавишный
- выключатель двухклавишный (флажков — по числу клавиш)
- выключатель с проходной или перекрёстной клавишей (обратный флажок); тип клавиши — в подписи
- привязки точек и выводов от угла и от пола, мм
- мебель и приборы — фасад по расстановке (условно)
- дверь скрытого монтажа: полотно в плоскости стены (узел — на листе узлов)
- стены и перекрытия в сечении
- окраска: тон — цвет по коду производителя (условно)
- О1 — марка отделки по реестру отделки альбома
- А — марка развёртки: буква стены, стрелка — взгляд

Ведомость отделки (на листе)

Марка	Поверхность	Материал, изделие	Цвет, код	Кол.
О10	плинтус	плинтус МДФ, h 80 мм, аналог: плинтус МДФ под окраску 80×16 мм, полуглянцевая	Farrow & Ball No. 291 «School House White тёплый меловой белый»	1,8 м
О13	стены	окраска, Tikkurila Luja 7, шелковисто-матовая, подготовка К3	Farrow & Ball No. 291 «School House White тёплый меловой белый»	5,2 м²
О15	потолок	окраска, Tikkurila Luja 7, матовая, подготовка Q3	Farrow & Ball No. 291 «School House White тёплый меловой белый»	6,5 м²

Допущения и предложения на листе

Основа листа: размеры сняты со скана обмерного плана KV design (см): часть подписей не читается, помещения выровнены по читаемым размерам; контрольный обмер не выполнен (К-1); высота потолка 2650 мм принята по отметкам обмера (Н = 2,50…2,66 м, ригель 2,28 м) — уточнить при обмере (К-2); толщины стен 300 / 120 мм приняты, межквартирная стена и колонны — по скану, не замерены (К-1); разрешённая мощность 15 кВт принята по типовым ТУ; при объединении двух квартир — переоформление ТУ (К-4).

Знак «**» — предложение проектировщика, заказчиком не утверждено (согласовать с заказчиком): записи в реестре нет: Р17 — высота 1700 мм выше нормы 1 м (ПУЭ 6.6.30) по назначению: питание слаботочного щита ЩС, рядом со щитом на его высоте; Р21 — высота 2200 мм выше нормы 1 м (ПУЭ 6.6.30) по назначению: питание вытяжки М25, розетка в модуле за съёмной панелью; ЭВ4 — по образцу: Добавлены выводы к вентиляторам: ЭВ4 (ВР1, ванная) и ЭВ5 (ВР3, санузел 2) — группа 3, высота 2389 мм, включение с основным светом, таймер выбега в вентиляторе; и коробки уравнивания потенциалов КУП1 (ванная) и КУП2 (санузел 2) — высота 300 мм, у входа, вне зон 0–2, проводник от шины PE щита ЩК, сече.

См. лист открытых вопросов (лист 6, записи К-1, К-2, К-4).

Примечания

1. Развёртки — вид на стену изнутри помещения, по часовой стрелке; расположение — на схеме листа и на листе 65; размеры — в мм по чистовым поверхностям; отметки — в м от ±0,000; высоты Н — от чистого пола помещения до оси изделия, у декора — до центра.
2. Красные цепочки — привязки электроточек и выводов: по горизонтали от угла чистовых стен, по вертикали от чистого пола, до оси изделия; звенья короче 3 мм на листе вынесены во второй ярус (ближняя к стене цепочка).
3. У знака электроточки: марка (Р — розетка, S — выключатель, Св — светильник, ЭВ — вывод кабеля), ×N — число постов в рамке, гр. — группа щита, Н — высота оси от чистого пола, мм; группы по клавишам выключателя — на листе выключателей.
4. Схема мебели, приборов и декора не является технической документацией для производства мебели; габариты — по паспортам изделий.
5. Двери скрытого монтажа — полотно в плоскости стены, отделка стены по полотну, плинтус прерывается у короба (узел — на листе узлов).
6. Выводы кухонной техники — по утверждённому проекту кухни: привязки выводов даются от осей модулей гарнитура.

1000 мм · печать 1:1

Изм.	Кол.уч	Лист	№ док.	Подп.	Дата
Разраб.		Кырлан А.С.			18.10.26
Пров.					
ГИП					
Н. контр.					
Утв.					

ГД-2026-009-АИ

Квартира 103 м²

Общая площадь 100,72* м² · * размеры со скана, не замерены (реестр — л. 6, К-1)

Дизайн-проект интерьера

Стадия	Лист	Листов
РП	73	96

Развёртка стены А. Кухня (пом. 5), кухонный фронт

М 1:20

Кырлан Александр Сергеевич

выпуск 18.10.2026 № 53dc234b8d · стр. 84 из 135

Развёртка стены Б. Кухня (пом. 5), кухонный фронт

Кухня (пом. 5) · вид изнутри помещения · размеры в мм, отметки в м

ПРЕДВАРИТЕЛЬНО · не для производства работ · открыто пунктов: 4 (реестр — л. 6)

Развёртка стены Б

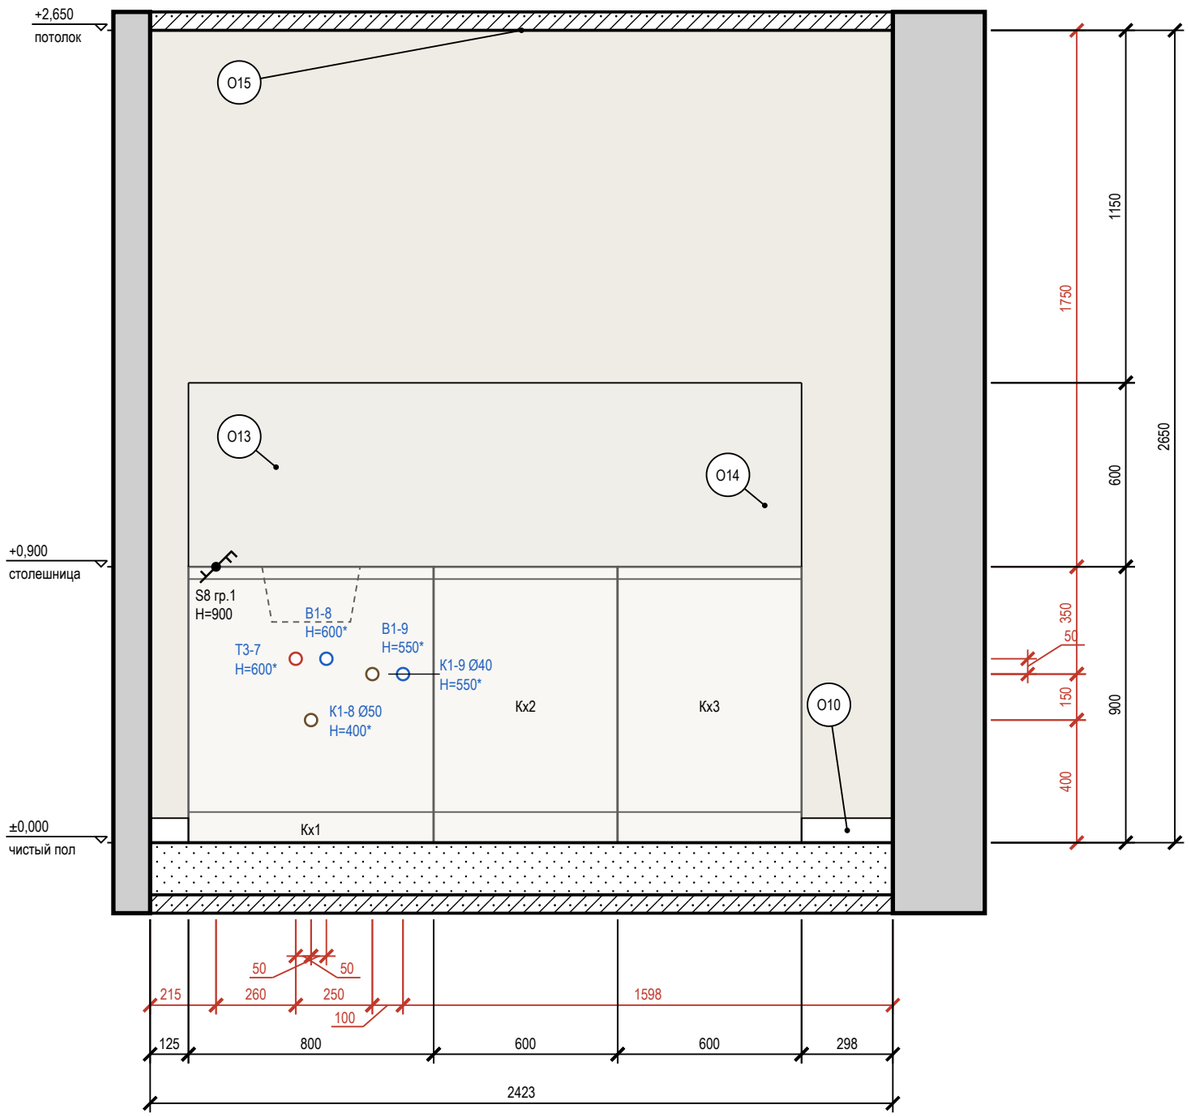

Схема развёрток (М 1:100)

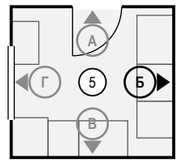

Условные обозначения

- выключатель одноклавишный
- выключатель двухклавишный (флажков — по числу клавиш)
- выключатель с проходной или перекрёстной клавишей (обратный флажок); тип клавиши — в подписи
- вывод В1 (код — в ведомости привязок)
- вывод Т3 (код — в ведомости привязок)
- вывод К1 (код — в ведомости привязок)
- привязки точек и выводов от угла и от пола, мм
- мебель и приборы — фасад по расстановке (условно)
- стены и перекрытия в сечении
- плитка: сетка швов по формату, ▲ — ось старта
- окраска: тон — цвет по коду производителя (условно)
- О1 — марка отделки по реестру отделки альбома
- А — марка развёртки: буква стены, стрелка — взгляд

Ведомость отделки (на листе)

Марка	Поверхность	Материал, изделие	Цвет, код	Кол.
О10	плинтус	плинтус МДФ, h 80 мм, аналог: плинтус МДФ под окраску 80×16 мм, полуглянцевая	Farrow & Ball No. 291 «School House White тёплый меловой белый»	0,4 м
О13	стены	окраска, Tikkurila Luja 7, шелковисто-матовая, подготовка К3	Farrow & Ball No. 291 «School House White тёплый меловой белый»	5,2 м²
О14	фартук	керамогранит, аналог: керамогранит матовый, тон F497, затирка CG2WA	#F1F1EC «тон Paper F497»	1,2 м²
О15	потолок	окраска, Tikkurila Luja 7, матовая, подготовка Q3	Farrow & Ball No. 291 «School House White тёплый меловой белый»	6,5 м²

Допущения и предложения на листе

Основа листа: размеры сняты со скана обмерного плана KV design (см): часть подписей не читается, помещения выровнены по читаемым размерам; контрольный обмер не выполнен (К-1); высота потолка 2650 мм принята по отметкам обмера (Н = 2,50…2,66 м, ригель 2,28 м) — уточнить при обмере (К-2); толщины стен 300 / 120 мм приняты, межквартирная стена и колонны — по скану, не замерены (К-1); разрешённая мощность 15 кВт принята по типовым ТУ; при объединении двух квартир — переоформление ТУ (К-4).
См. лист открытых вопросов (лист 6, записи К-1, К-2, К-4).

Примечания

1. Развёртки — вид на стену изнутри помещения, по часовой стрелке; расположение — на схеме листа и на листе 65; размеры — в мм по чистовым поверхностям; отметки — в м от ±0,000; высоты Н — от чистого пола помещения до оси изделия, у декора — до центра.
2. Красные цепочки — привязки электроточек и выводов: по горизонтали от угла чистовых стен, по вертикали от чистого пола, до оси изделия; звенья короче 3 мм на листе вынесены во второй ярус (ближняя к стене цепочка).
3. У знака электроточки: марка (Р — розетка, S — выключатель, Св — светильник, ЭВ — вывод кабеля), ×N — число постов в рамке, гр. — группа щита, Н — высота оси от чистого пола, мм; группы по клавишам выключателя — на листе выключателей.
4. Схема мебели, приборов и декора не является технической документацией для производства мебели; габариты — по паспортам изделий.
5. Выводы ВК — коды и высоты по листу выводов сантехники; * — высота принята по типовой практике монтажа, окончательно — по паспорту прибора.
6. Выводы кухонной техники — по утверждённому проекту кухни: привязки выводов даются от осей модулей гарнитура.

1000 мм · печать 1:1

Изм.	Кол.уч	Лист	№ док.	Подп.	Дата
Разраб.		Кырлан А.С.			18.10.26
Пров.					
ГИП					
Н. контр.					
Утв.					

ГД-2026-009-АИ

Квартира 103 м²

Общая площадь 100,72* м² · * размеры со скана, не замерены (реестр — л. 6, К-1)

Дизайн-проект интерьера

Стадия	Лист	Листов
РП	74	96

Развёртка стены Б. Кухня (пом. 5), кухонный фронт

М 1:20

Кырлан Александр Сергеевич

выпуск 18.10.2026 № 53dc234b8d · стр. 85 из 135

Развёртка стены В. Кухня (пом. 5), кухонный фронт

Кухня (пом. 5) · вид изнутри помещения · размеры в мм, отметки в м

ПРЕДВАРИТЕЛЬНО · не для производства работ · открыто пунктов: 4 (реестр — л. 6)

Развёртка стены В

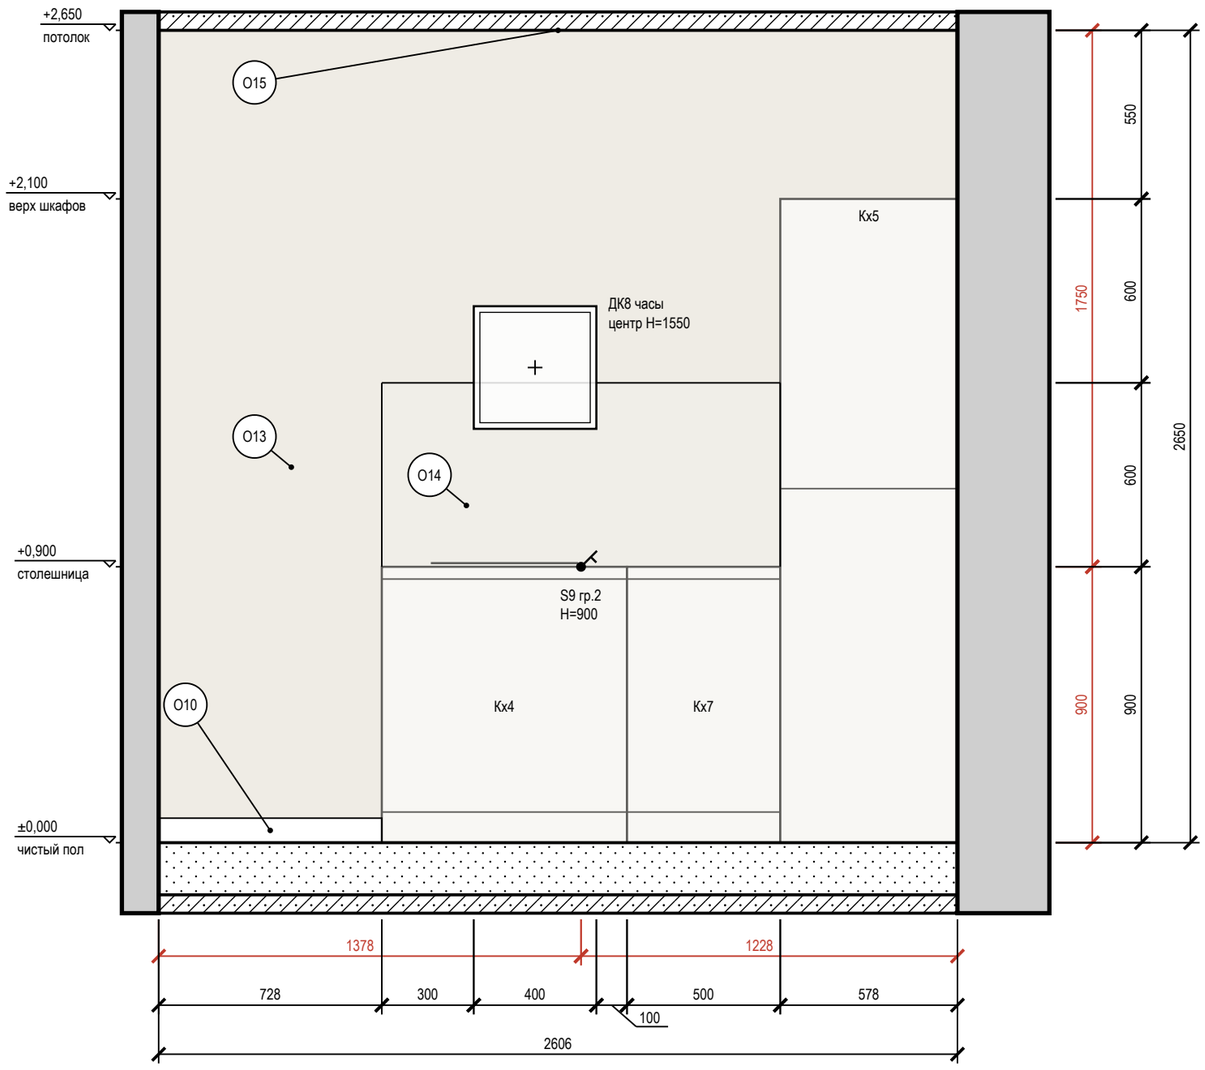

Схема развёрток (М 1:100)

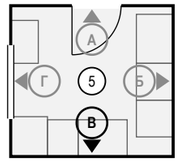

Условные обозначения

- выключатель одноклавишный
- привязки точек и выводов от угла и от пола, мм
- мебель и приборы — фасад по расстановке (условно)
- картина (декор): марка Д, крест — центр, Н — высота центра, мм
- стены и перекрытия в сечении
- плитка: сетка швов по формату, ▲ — ось старта
- окраска: тон — цвет по коду производителя (условно)
- О1 — марка отделки по реестру отделки альбома
- А — марка развёртки: буква стены, стрелка — взгляд

Ведомость отделки (на листе)

Марка	Поверхность	Материал, изделие	Цвет, код	Кол.
О10	плинтус	плинтус МДФ, h 80 мм, аналог: плинтус МДФ под окраску 80×16 мм, полуглянцевая	Farrow & Ball No. 291 «School House White — тёплый меловой белый»	0,7 м
О13	стены	окраска, Tikkurila Luja 7, шелковисто-матовая, подготовка К3	Farrow & Ball No. 291 «School House White — тёплый меловой белый»	6,1 м²
О14	фартук	керамогранит, аналог: керамогранит матовый, тон F497, затирка CG2WA	#F1F1EC «тон Paper F497»	0,8 м²
О15	потолок	окраска, Tikkurila Luja 7, матовая, подготовка Q3	Farrow & Ball No. 291 «School House White — тёплый меловой белый»	6,5 м²

Допущения и предложения на листе

Основа листа: размеры сняты со скана обмерного плана KV design (см): часть подписей не читается, помещения выровнены по читаемым размерам; контрольный обмер не выполнен (К-1); высота потолка 2650 мм принята по отметкам обмера (Н = 2,50…2,66 м, ригель 2,28 м) — уточнить при обмере (К-2); толщины стен 300 / 120 мм приняты, межквартирная стена и колонны — по скану, не замерены (К-1); разрешённая мощность 15 кВт принята по типовым ТУ; при объединении двух квартир — переоформление ТУ (К-4).

См. лист открытых вопросов (лист 6, записи К-1, К-2, К-4).

Примечания

1. Развёртки — вид на стену изнутри помещения, по часовой стрелке; расположение — на схеме листа и на листе 65; размеры — в мм по чистовым поверхностям; отметки — в м от ±0,000; высоты Н — от чистого пола помещения до оси изделия, у декора — до центра.
2. Красные цепочки — привязки электроточек и выводов: по горизонтали от угла чистовых стен, по вертикали от чистого пола, до оси изделия; звенья короче 3 мм на листе вынесены во второй ярус (ближняя к стене цепочка).
3. У знака электроточки: марка (Р — розетка, S — выключатель, Св — светильник, ЭВ — вывод кабеля), ×N — число постов в рамке, гр. — группа щита, Н — высота оси от чистого пола, мм; группы по клавишам выключателя — на листе выключателей.
4. Схема мебели, приборов и декора не является технической документацией для производства мебели; габариты — по паспортам изделий.
5. Картины и зеркала крепить к основанию по паспорту изделия (закладные и анкеры — в перечне скрытых работ); крест — ось центра предмета.
6. Выводы кухонной техники — по утверждённому проекту кухни: привязки выводов даются от осей модулей гарнитура.

1000 мм · печать 1:1

Изм.	Кол.уч	Лист	№ док.	Подп.	Дата
Разраб.		Кырлан А.С.			18.10.26
Пров.					
ГИП					
Н. контр.					
Утв.					

ГД-2026-009-АИ

Квартира 103 м²

Общая площадь 100,72* м² · * размеры со скана, не замерены (реестр — л. 6, К-1)

Дизайн-проект интерьера	Стадия	Лист	Листов
	РП	75	96

Развёртка стены В. Кухня (пом. 5), кухонный фронт

М 1:20

Кырлан Александр Сергеевич

выпуск 18.10.2026 № 53dc234b8d · стр. 86 из 135

Развёртка стены Г. Кухня (пом. 5)

Кухня (пом. 5) · вид изнутри помещения · размеры в мм, отметки в м

ПРЕДВАРИТЕЛЬНО · не для производства работ · открыто пунктов: 4 (реестр — л. 6)

Развёртка стены Г

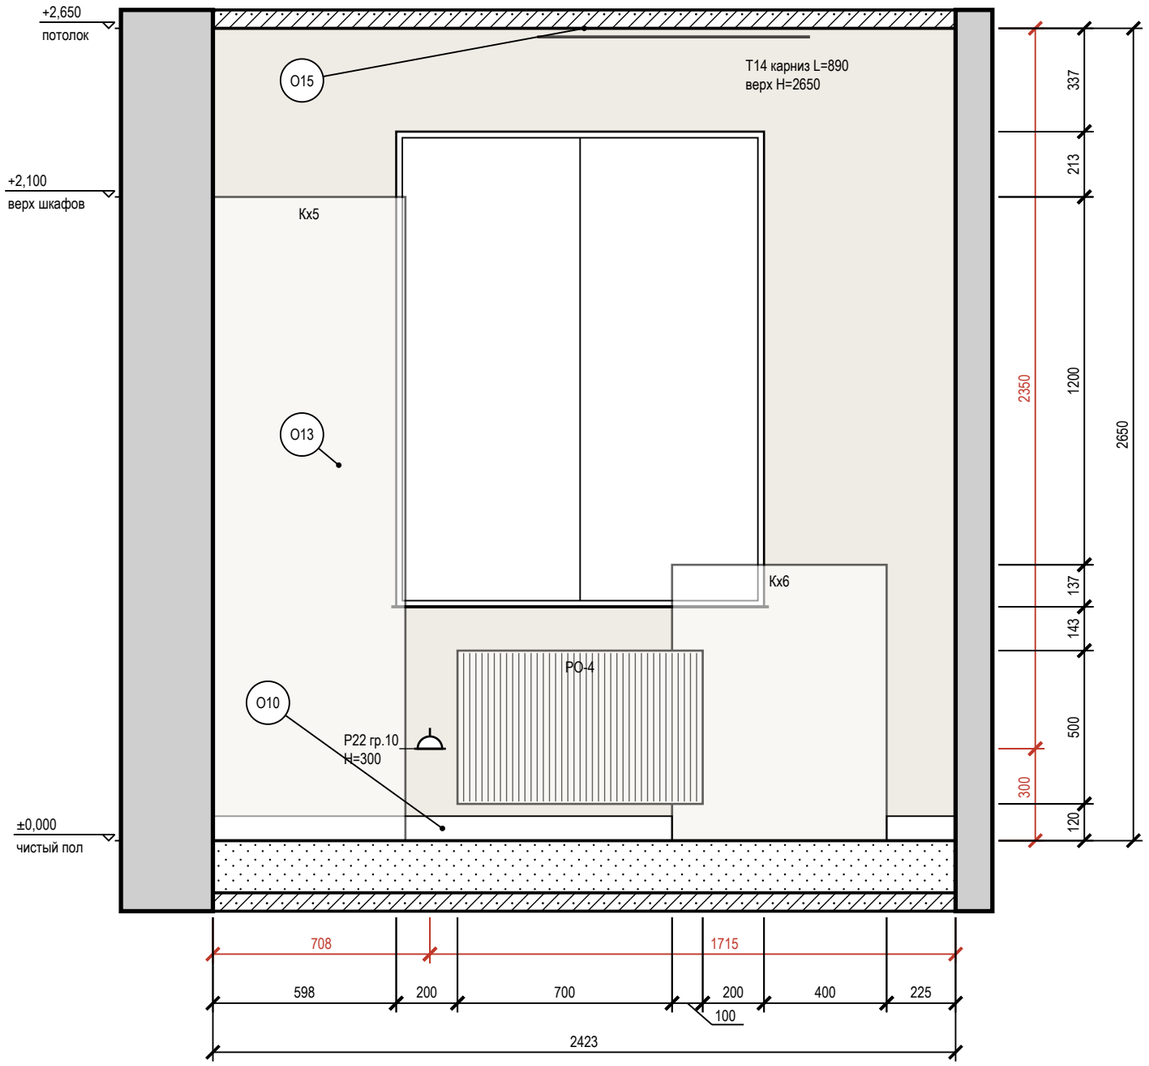

Схема развёрток (М 1:100)

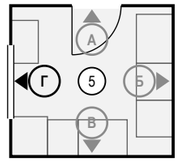

Условные обозначения

- розетка с заземляющим контактом; у знака — марка, ×N постов в рамке, гр. — группа щита, Н — высота оси, мм
- привязки точек и выводов от угла и от пола, мм
- мебель и приборы — фасад по расстановке (условно)
- карниз (шина) и шторы в собранном виде: марка Т, длина L, верх Н
- окно: проём, рама, подоконник
- радиатор отопления; марка — по плану отопления
- стены и перекрытия в сечении
- окраска: тон — цвет по коду производителя (условно)
- О1 — марка отделки по реестру отделки альбома
- А — марка развёртки: буква стены, стрелка — взгляд

Ведомость отделки (на листе)

Марка	Поверхность	Материал, изделие	Цвет, код	Кол.
О10	плинтус	плинтус МДФ, h 80 мм, аналог: плинтус МДФ под окраску 80×16 мм, полуглянцевая	Farrow & Ball No. 291 «School House White — тёплый меловой белый»	1,7 м
О13	стены	окраска, Tikkurila Luja 7, шелковисто-матовая, подготовка К3	Farrow & Ball No. 291 «School House White — тёплый меловой белый»	4,6 м²
О15	потолок	окраска, Tikkurila Luja 7, матовая, подготовка Q3	Farrow & Ball No. 291 «School House White — тёплый меловой белый»	6,5 м²

Допущения и предложения на листе

Основа листа: размеры сняты со скана обмерного плана KV design (см): часть подписей не читается, помещения выровнены по читаемым размерам; контрольный обмер не выполнен (К-1); высота потолка 2650 мм принята по отметкам обмера (Н = 2,50…2,66 м, ригель 2,28 м) — уточнить при обмере (К-2); толщины стен 300 / 120 мм приняты, межквартирная стена и колонны — по скану, не замерены (К-1); разрешённая мощность 15 кВт принята по типовым ТУ; при объединении двух квартир — переоформление ТУ (К-4).

См. лист открытых вопросов (лист 6, записи К-1, К-2, К-4).

Примечания

1. Развёртки — вид на стену изнутри помещения, по часовой стрелке; расположение — на схеме листа и на листе 65; размеры — в мм по чистовым поверхностям; отметки — в м от ±0,000; высоты Н — от чистого пола помещения до оси изделия, у декора — до центра.
2. Красные цепочки — привязки электроточек и выводов: по горизонтали от угла чистовых стен, по вертикали от чистого пола, до оси изделия; звенья короче 3 мм на листе вынесены во второй ярус (ближняя к стене цепочка).
3. У знака электроточки: марка (Р — розетка, S — выключатель, Св — светильник, ЭВ — вывод кабеля), ×N — число постов в рамке, гр. — группа щита, Н — высота оси от чистого пола, мм; группы по клавишам выключателя — на листе выключателей.
4. Схема мебели, приборов и декора не является технической документацией для производства мебели; габариты — по паспортам изделий.
5. Карнизы (шины) — по ведомости текстиля декоратора; длина L и верх Н — по развёртке, крепление — до окраски потолка.

1000 мм · печать 1:1

Изм.	Кол.уч	Лист	№ док.	Подп.	Дата
Разраб.		Кырлан А.С.			18.10.26
Пров.					
ГИП					
Н. контр.					
Утв.					

ГД-2026-009-АИ

Квартира 103 м²

Общая площадь 100,72* м² · * размеры со скана, не замерены (реестр — л. 6, К-1)

Дизайн-проект интерьера

Стадия	Лист	Листов
РП	76	96

Развёртка стены Г. Кухня (пом. 5)

М 1:20

Кырлан Александр Сергеевич

выпуск 18.10.2026 № 53dc234b8d · стр. 87 из 135

Развёртки стен А, Б. Ванная (пом. 6)

Ванная (пом. 6) · вид изнутри помещения · размеры в мм, отметки в м

ПРЕДВАРИТЕЛЬНО · не для производства работ · открыто пунктов: 4 (реестр — л. 6)

Развёртка стены А

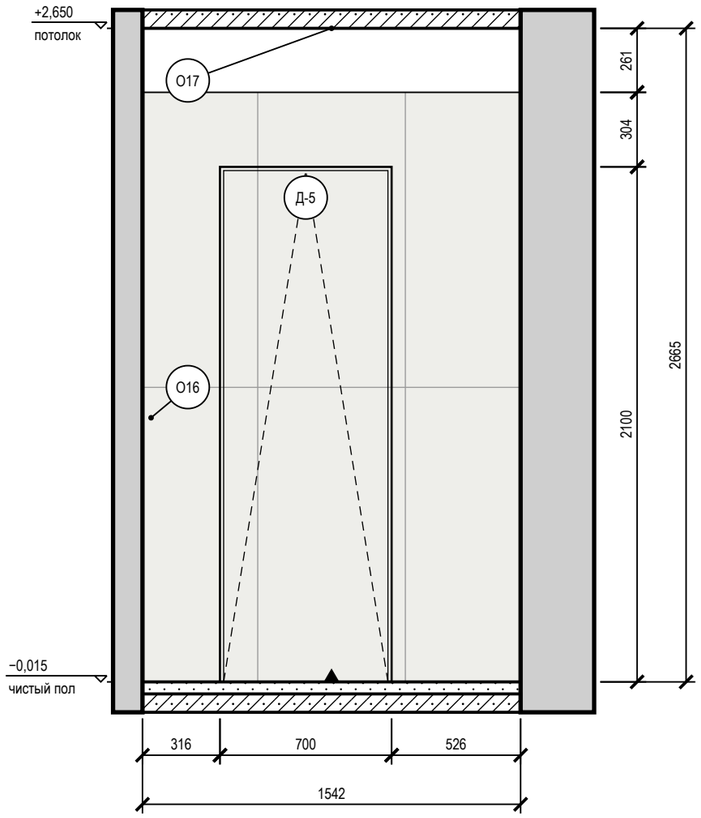

Развёртка стены Б

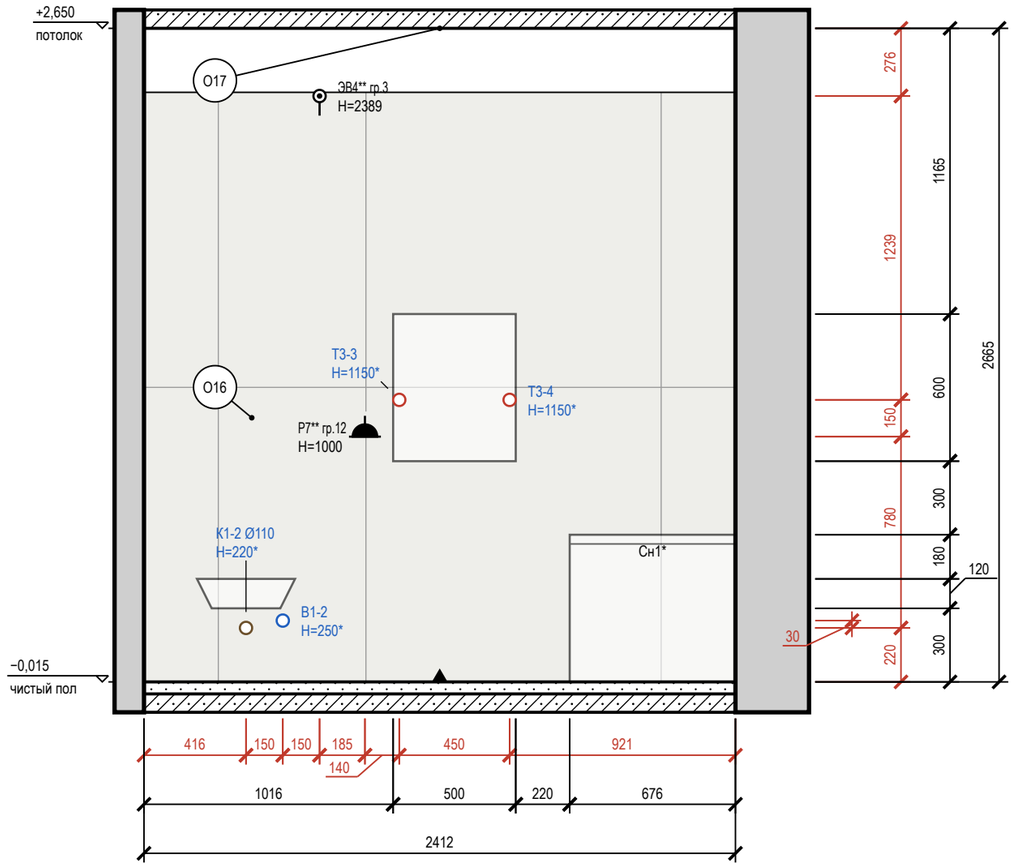

Условные обозначения

- розетка влагозащищённая IP44
- вывод кабеля для подключения прибора (без розетки), марка ЭВ
- вывод В1 (код — в ведомости привязок)
- вывод Т3 (код — в ведомости привязок)
- вывод К1 (код — в ведомости привязок)
- привязки точек и выводов от угла и от пола, мм
- мебель и приборы — фасад по расстановке (условно)
- дверь скрытого монтажа: полотно в плоскости стены (узел — на листе узлов)
- стены и перекрытия в сечении
- плитка: сетка швов по формату, ▲ — ось старта
- О1 — марка отделки по реестру отделки альбома
- А — марка развёртки: буква стены, стрелка — взгляд

Схема развёрток (М 1:100)

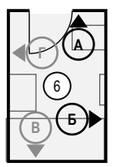

Ведомость отделки (на листе)

Марка	Поверхность	Материал, изделие	Цвет, код	Кол.
О16	стены	облицовка плиткой, Atlas Concorde Marvel Travertine, 600×1200×9 мм, A8UZ, затирка CG2WA	Atlas Concorde A8UZ «Marvel Travertine»	8 м²
О17	потолок	окраска, Tikkurila Luja 7, матовая, подготовка Q3	NCS S 0502-Y «Белый с лёгкой желтизной»	3,9 м²

Допущения и предложения на листе

Основа листа: размеры сняты со скана обмерного плана KV design (см): часть подписей не читается, помещения выровнены по читаемым размерам; контрольный обмер не выполнен (К-1); высота потолка 2650 мм принята по отметкам обмера (Н = 2,50…2,66 м, ригель 2,28 м) — уточнить при обмере (К-2); толщины стен 300 / 120 мм приняты, межквартирная стена и колонны — по скану, не замерены (К-1); разрешённая мощность 15 кВт принята по типовым ТУ; при объединении двух квартир — переоформление ТУ (К-4).
Знак «**» — предложение проектировщика, заказчиком не утверждено (согласовать с заказчиком): записи в реестре нет: Р7 — по образцу: Р7, Р8 и Р33 на высоте 1000 мм — верхний предел нормы (ПУЭ, п. 6.6.30, не выше 1 м); флаг решения снят; ЭВ4 — по образцу: Добавлены выводы к вентиляторам: ЭВ4 (ВР1, ванная) и ЭВ5 (ВР3, санузел 2) — группа 3, высота 2389 мм, включение с основным светом, таймер выбега в вентиляторе; и коробки уравнивания потенциалов КУП1 (ванная) и КУП2 (санузел 2) — высота 300 мм, у входа, вне зон 0–2, проводник от шины PE щита ЩК, сече.
См. лист открытых вопросов (лист 6, записи К-1, К-2, К-4).

Примечания

1. Развёртки — вид на стену изнутри помещения, по часовой стрелке; расположение — на схеме листа и на листе 65; размеры — в мм по чистовым поверхностям; отметки — в м от ±0,000; высоты Н — от чистого пола помещения до оси изделия, у декора — до центра.
2. Красные цепочки — привязки электроточек и выводов: по горизонтали от угла чистовых стен, по вертикали от чистого пола, до оси изделия; звенья короче 3 мм на листе вынесены во второй ярус (ближняя к стене цепочка).
3. У знака электроточки: марка (Р — розетка, S — выключатель, Св — светильник, ЭВ — вывод кабеля), ×N — число постов в рамке, гр. — группа щита, Н — высота оси от чистого пола, мм; группы по клавишам выключателя — на листе выключателей.
4. Схема мебели, приборов и декора не является технической документацией для производства мебели; габариты — по паспортам изделий (* — высота не задана в проекте, показана по типовому изделию).
5. Выводы ВК — коды и высоты по листу выводов сантехники; * — высота принята по типовой практике монтажа, окончательно — по паспорту прибора.
6. Облицовка — по сетке швов 2 мм, раскладка от оси стены (треугольник у пола); целые ряды от пола; подрезки — по листу раскладки плитки.
7. Гидроизоляция в 2 слоя, заход на стены 200 мм — до облицовки, с актом скрытых работ и тестом проливом (узел — на листе узлов).
8. Двери скрытого монтажа — полотно в плоскости стены, отделка стены по полотну, плинтус прерывается у короба (узел — на листе узлов).
9. Линии узора (швы плитки, складки штор, рёбра радиаторов) прерываются у знаков и выносок — просвет между линиями не менее 0,7 мм.

1000 мм · печать 1:1

Изм.	Кол.уч	Лист	№ док.	Подп.	Дата
Разраб.		Кырлан А.С.			18.10.26
Пров.					
ГИП					
Н. контр.					
Утв.					

ГД-2026-009-АИ

Квартира 103 м²

Общая площадь 100,72* м² · * размеры со скана, не замерены (реестр — л. 6, К-1)

Дизайн-проект интерьера

Стадия	Лист	Листов
РП	77	96

Развёртки стен А, Б. Ванная (пом. 6)

М 1:25

Кырлан Александр Сергеевич

выпуск 18.10.2026 № 53dc2348d8d · стр. 88 из 135

Развёртка стены В. Ванная (пом. 6)

Ванная (пом. 6) · вид изнутри помещения · размеры в мм, отметки в м

ПРЕДВАРИТЕЛЬНО · не для производства работ · открыто пунктов: 4 (реестр — л. 6)

Развёртка стены В

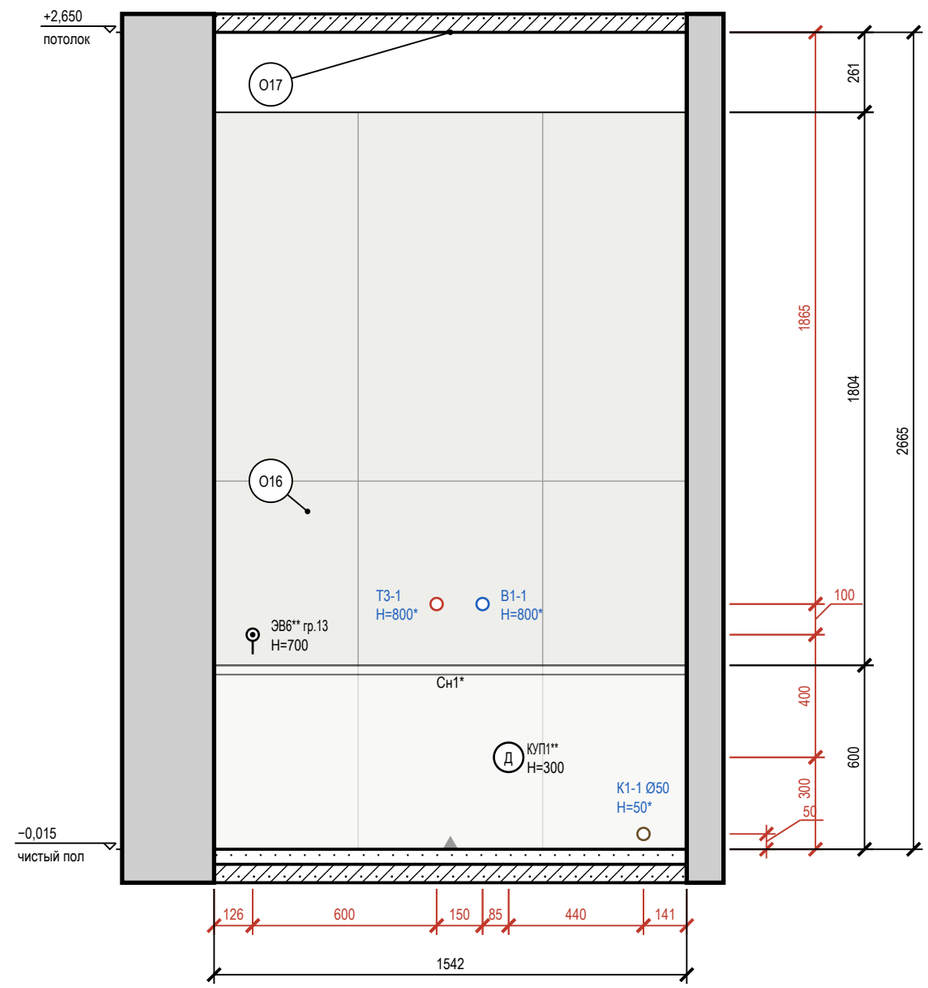

Схема развёрток (М 1:100)

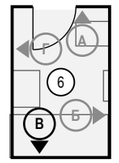

Условные обозначения

- вывод кабеля для подключения прибора (без розетки), марка ЭВ
- вывод В1 (код — в ведомости привязок)
- вывод Т3 (код — в ведомости привязок)
- вывод К1 (код — в ведомости привязок)
- привязки точек и выводов от угла и от пола, мм
- мебель и приборы — фасад по расстановке (условно)
- стены и перекрытия в сечении
- плитка: сетка швов по формату, ▲ — ось старта
- О1 — марка отделки по реестру отделки альбома
- А — марка развёртки: буква стены, стрелка — взгляд

Ведомость отделки (на листе)

Марка	Поверхность	Материал, изделие	Цвет, код	Кол.
О16	стены	облицовка плиткой, Atlas Concorde Marvel Travertine, 600×1200×9 мм, A8UZ, затирка CG2WA	Atlas Concorde A8UZ «Marvel Travertine»	3,7 м²
О17	потолок	окраска, Tikkurila Luja 7, матовая, подготовка Q3	NCS S 0502-Y «Белый с лёгкой желтизной»	3,9 м²

Допущения и предложения на листе

Основа листа: размеры сняты со скана обмерного плана KV design (см): часть подписей не читается, помещения выровнены по читаемым размерам; контрольный обмер не выполнен (К-1); высота потолка 2650 мм принята по отметкам обмера (Н = 2,50…2,66 м, ригель 2,28 м) — уточнить при обмере (К-2); толщины стен 300 / 120 мм приняты, межквартирная стена и колонны — по скану, не замерены (К-1); разрешённая мощность 15 кВт принята по типовым ТУ; при объединении двух квартир — переоформление ТУ (К-4).

Знак «**» — предложение проектировщика, заказчиком не утверждено (согласовать с заказчиком): записи в реестре нет: КУП1 — по образцу: Добавлены выводы к вентиляторам: ЭВ4 (ВР1, ванная) и ЭВ5 (ВР3, санузел 2) — группа 3, высота 2389 мм, включение с основным светом, таймер выбега в вентиляторе; и коробки уравнивания потенциалов КУП1 (ванная) и КУП2 (санузел 2) — высота 300 мм, у входа, вне зон 0–2, проводник от шины PE щита ЩК, сече; ЭВ6 — по образцу: Добавлены электрические полотенцесушители IP44: П10 в ванной (480 мм, низ 900 мм) и П13 в санузле 2 (400 мм, низ 900 мм), выводы ЭВ6 и ЭВ7; мощность группы 13 — 2,4 кВт вместо 1,8 кВт.

См. лист открытых вопросов (лист 6, записи К-1, К-2, К-4).

Примечания

1. Развёртки — вид на стену изнутри помещения, по часовой стрелке; расположение — на схеме листа и на листе 65; размеры — в мм по чистовым поверхностям; отметки — в м от ±0,000; высоты Н — от чистого пола помещения до оси изделия, у декора — до центра.
2. Красные цепочки — привязки электроточек и выводов: по горизонтали от угла чистовых стен, по вертикали от чистого пола, до оси изделия; звенья короче 3 мм на листе вынесены во второй ярус (ближняя к стене цепочка).
3. У знака электроточки: марка (Р — розетка, S — выключатель, Св — светильник, ЭВ — вывод кабеля), ×N — число постов в рамке, гр. — группа щита, Н — высота оси от чистого пола, мм; группы по клавишам выключателя — на листе выключателей.
4. Схема мебели, приборов и декора не является технической документацией для производства мебели; габариты — по паспортам изделий (* — высота не задана в проекте, показана по типовому изделию).
5. Выводы ВК — коды и высоты по листу выводов сантехники; * — высота принята по типовой практике монтажа, окончательно — по паспорту прибора.
6. Облицовка — по сетке швов 2 мм, раскладка от оси стены (треугольник у пола), целые ряды от пола; подрезки — по листу раскладки плитки.
7. Гидроизоляция в 2 слоя, заход на стены 200 мм — до облицовки, с актом скрытых работ и тестом проливом (узел — на листе узлов).

1000 мм · печать 1:1

Изм.	Кол.уч	Лист	№ док.	Подп.	Дата
Разраб.		Кырлан А.С.			18.10.26
Пров.					
ГИП					
Н. контр.					
Утв.					

ГД-2026-009-АИ

Квартира 103 м²

Общая площадь 100,72* м² · * размеры со скана, не замерены (реестр — л. 6, К-1)

Дизайн-проект интерьера

Стадия	Лист	Листов
РП	78	96

Развёртка стены В. Ванная (пом. 6)

М 1:20

Кырлан Александр Сергеевич

выпуск 18.10.2026 № 53dc234b8d · стр. 89 из 135

Развёртка стены Г. Ванная (пом. 6)

Ванная (пом. 6) · вид изнутри помещения · размеры в мм, отметки в м

ПРЕДВАРИТЕЛЬНО · не для производства работ · открыто пунктов: 4 (реестр — л. 6)

Развёртка стены Г

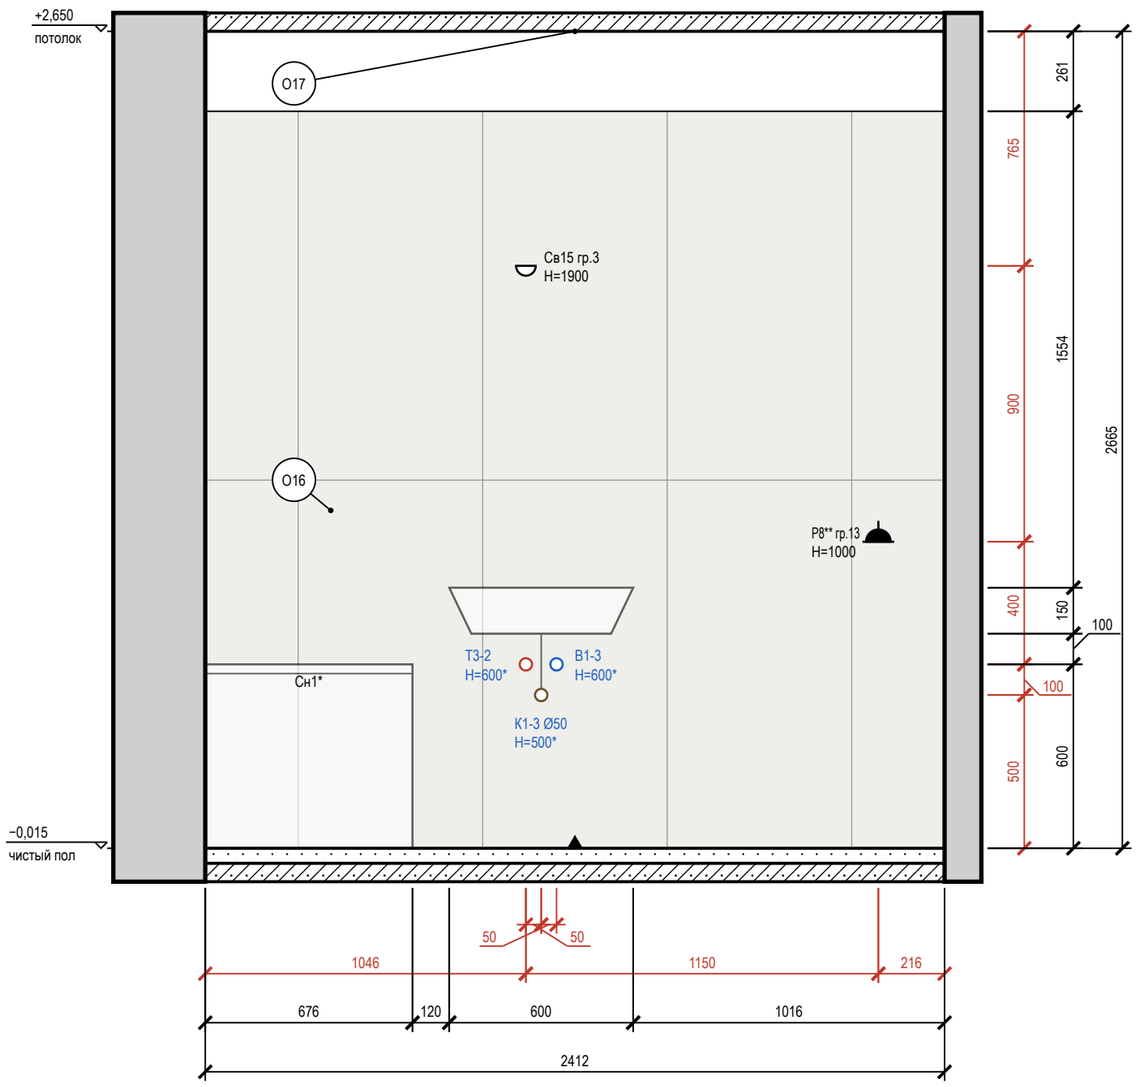

Схема развёрток (М 1:100)

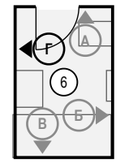

Условные обозначения

- розетка влагозащищённая IP44
- светильник настенный (бра), H — высота оси
- вывод В1 (код — в ведомости привязок)
- вывод Т3 (код — в ведомости привязок)
- вывод К1 (код — в ведомости привязок)
- привязки точек и выводов от угла и от пола, мм
- мебель и приборы — фасад по расстановке (условно)
- стены и перекрытия в сечении
- плитка: сетка швов по формату, ▲ — ось старта
- О1 — марка отделки по реестру отделки альбома
- А — марка развёртки: буква стены, стрелка — взгляд

Ведомость отделки (на листе)

Марка	Поверхность	Материал, изделие	Цвет, код	Кол.
О16	стены	облицовка плиткой, Atlas Concorde Marvel Travertine, 600×1200×9 мм, A8UZ, затирка CG2WA	Atlas Concorde A8UZ «Marvel Travertine»	5,8 м²
О17	потолок	окраска, Tikkurila Luja 7, матовая, подготовка Q3	NCS S 0502-Y «Белый с лёгкой желтизной»	3,9 м²

Допущения и предложения на листе

Основа листа: размеры сняты со скана обмерного плана KV design (см): часть подписей не читается, помещения выровнены по читаемым размерам; контрольный обмер не выполнен (К-1); высота потолка 2650 мм принята по отметкам обмера (Н = 2,50…2,66 м, ригель 2,28 м) — уточнить при обмере (К-2); толщины стен 300 / 120 мм приняты, межквартирная стена и колонны — по скану, не замерены (К-1); разрешённая мощность 15 кВт принята по типовым ТУ; при объединении двух квартир — переоформление ТУ (К-4).

Знак «**» — предложение проектировщика, заказчиком не утверждено (согласовать с заказчиком): записи в реестре нет: Р8 — по образцу: Р7, Р8 и Р33 на высоте 1000 мм — верхний предел нормы (ПУЭ, п. 6.6.30, не выше 1 м); флаг решения снят.

См. лист открытых вопросов (лист 6, записи К-1, К-2, К-4).

Примечания

1. Развёртки — вид на стену изнутри помещения, по часовой стрелке; расположение — на схеме листа и на листе 65; размеры — в мм по чистовым поверхностям; отметки — в м от ±0,000; высоты Н — от чистого пола помещения до оси изделия, у декора — до центра.
2. Красные цепочки — привязки электроточек и выводов: по горизонтали от угла чистовых стен, по вертикали от чистого пола, до оси изделия; звенья короче 3 мм на листе вынесены во второй ярус (ближняя к стене цепочка).
3. У знака электроточки: марка (Р — розетка, S — выключатель, Св — светильник, ЭВ — вывод кабеля), ×N — число постов в рамке, гр. — группа щита, Н — высота оси от чистого пола, мм; группы по клавишам выключателя — на листе выключателей.
4. Схема мебели, приборов и декора не является технической документацией для производства мебели; габариты — по паспортам изделий (* — высота не задана в проекте, показана по типовому изделию).
5. Выводы ВК — коды и высоты по листу выводов сантехники; * — высота принята по типовой практике монтажа, окончательно — по паспорту прибора.
6. Облицовка — по сетке швов 2 мм, раскладка от оси стены (треугольник у пола), целые ряды от пола; подрезки — по листу раскладки плитки.
7. Гидроизоляция в 2 слоя, заход на стены 200 мм — до облицовки, с актом скрытых работ и тестом проливом (узел — на листе узлов).

1000 мм · печать 1:1

Изм.	Кол.уч	Лист	№ док.	Подп.	Дата
Разраб.		Кырлан А.С.			18.10.26
Пров.					
ГИП					
Н. контр.					
Утв.					

ГД-2026-009-АИ

Квартира 103 м²

Общая площадь 100,72* м² · * размеры со скана, не замерены (реестр — л. 6, К-1)

Дизайн-проект интерьера	Стадия	Лист	Листов
	РП	79	96

Развёртка стены Г. Ванная (пом. 6)

М 1:20

Кырлан Александр Сергеевич

выпуск 18.10.2026 № 53dc234b8d · стр. 90 из 135

Развёртки стен. Постирочная (пом. 7)

Постирочная (пом. 7) · вид изнутри помещения · размеры в мм, отметки в м

ПРЕДВАРИТЕЛЬНО · не для производства работ · открыто пунктов: 4 (реестр — л. 6)

Развёртка стены А

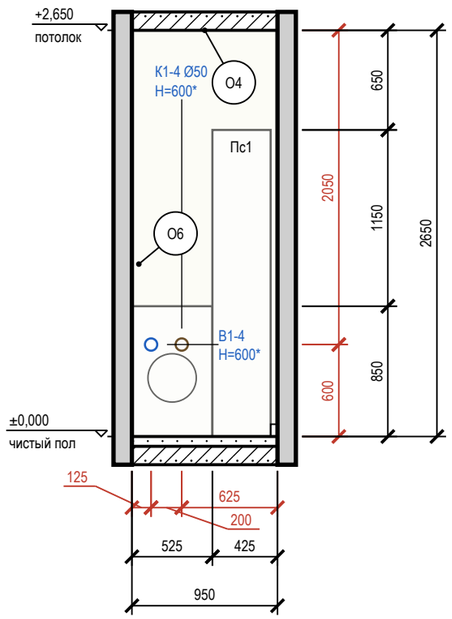

Развёртка стены Б

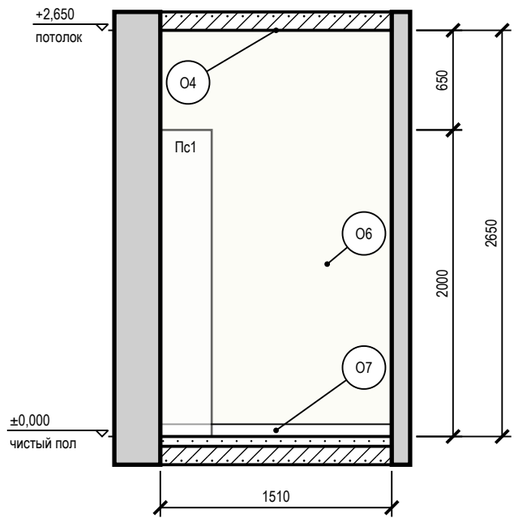

Развёртка стены В

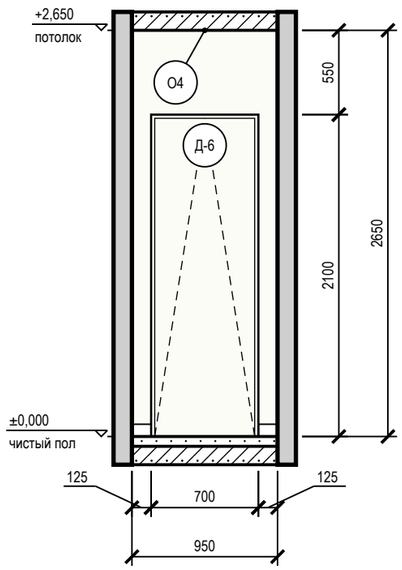

Развёртка стены Г

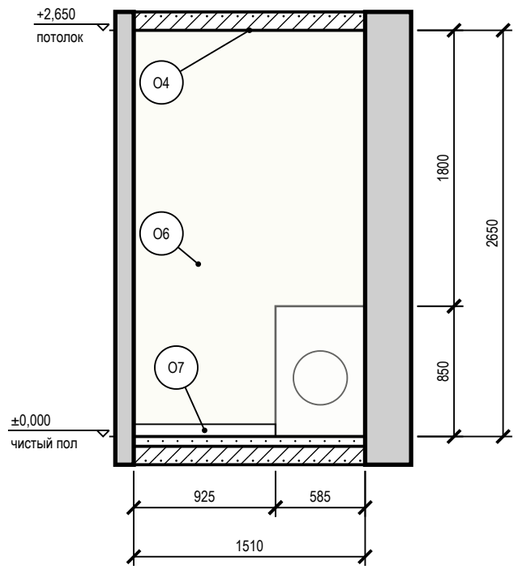

Схема развёрток (М 1:100)

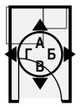

Условные обозначения

- вывод В1 (код — в ведомости привязок)
- вывод К1 (код — в ведомости привязок)
- привязки точек и выводов от угла и от пола, мм
- мебель и приборы — фасад по расстановке (условно)
- дверь скрытого монтажа: полотно в плоскости стены (узел — на листе узлов)
- стены и перекрытия в сечении
- окраска: тон — цвет по коду производителя (условно)
- О1 — марка отделки по реестру отделки альбома
- А — марка развёртки: буква стены, стрелка — взгляд

Ведомость отделки (на листе)

Марка	Поверхность	Материал, изделие	Цвет, код	Кол.
О4	потолок	окраска, Tikkurila Anti-Reflex 2, глубокоматовая, подготовка Q3	NCS S 0502-Y «Белый с лёгкой желтизной»	1,5 м²
О6	стены	окраска, Tikkurila Harmony, матовая, подготовка Q3	NCS S 0502-Y «Белый с лёгкой желтизной»	11,6 м²
О7	плинтус	плинтус МДФ, h 80 мм, аналог: плинтус МДФ под покраску 80×16	NCS S 0502-Y «Белый с лёгкой желтизной»	2,7 м

Допущения и предложения на листе

Основа листа: размеры сняты со скана обмерного плана KV design (см): часть подписей не читается, помещения выровнены по читаемым размерам; контрольный обмер не выполнен (К-1); высота потолка 2650 мм принята по отметкам обмера (Н = 2,50…2,66 м, ригель 2,28 м) — уточнить при обмере (К-2); толщины стен 300 / 120 мм приняты, межквартирная стена и колонны — по скану, не замерены (К-1); разрешённая мощность 15 кВт принята по типовым ТУ; при объединении двух квартир — переоформление ТУ (К-4).
См. лист открытых вопросов (лист 6, записи К-1, К-2, К-4).

Примечания

1. Развёртки — вид на стену изнутри помещения, по часовой стрелке; расположение — на схеме листа и на листе 65; размеры — в мм по чистовым поверхностям; отметки — в м от ±0,000; высоты Н — от чистого пола помещения до оси изделия, у декора — до центра.
2. Красные цепочки — привязки электроточек и выводов: по горизонтали от угла чистовых стен, по вертикали от чистого пола, до оси изделия; звенья короче 3 мм на листе вынесены во второй ярус (ближняя к стене цепочка).
3. У знака электроточки: марка (Р — розетка, S — выключатель, Св — светильник, ЭВ — вывод кабеля), ×N — число постов в рамке, гр. — группа щита, Н — высота оси от чистого пола, мм; группы по клавишам выключателя — на листе выключателей.
4. Схема мебели, приборов и декора не является технической документацией для производства мебели; габариты — по паспортам изделий (* — высота не задана в проекте, показана по типовому изделию).
5. Выводы ВК — коды и высоты по листу выводов сантехники; * — высота принята по типовой практике монтажа, окончательно — по паспорту прибора.
6. Двери скрытого монтажа — полотно в плоскости стены, отделка стены по полотну, плинтус прерывается у короба (узел — на листе узлов).

1000 мм · печать 1:1

Изм.	Кол.уч	Лист	№ док.	Подп.	Дата
Разраб.		Кырлан А.С.			18.10.26
Пров.					
ГИП					
Н. контр.					
Утв.					

ГД-2026-009-АИ

Квартира 103 м²

Общая площадь 100,72* м² · * размеры со скана, не замерены (реестр — л. 6, К-1)

Дизайн-проект интерьера

Стадия	Лист	Листов
РП	80	96

Развёртки стен. Постирочная (пом. 7)

М 1:40

Кырлан Александр Сергеевич

выпуск 18.10.2026 № 53dc2348d8d · стр. 91 из 135

Развёртки стен А, Б. Спальня 2 (пом. 8)

Спальня 2 (пом. 8) · вид изнутри помещения · размеры в мм, отметки в м

ПРЕДВАРИТЕЛЬНО · не для производства работ · открыто пунктов: 4 (реестр — л. 6)

Развёртка стены А

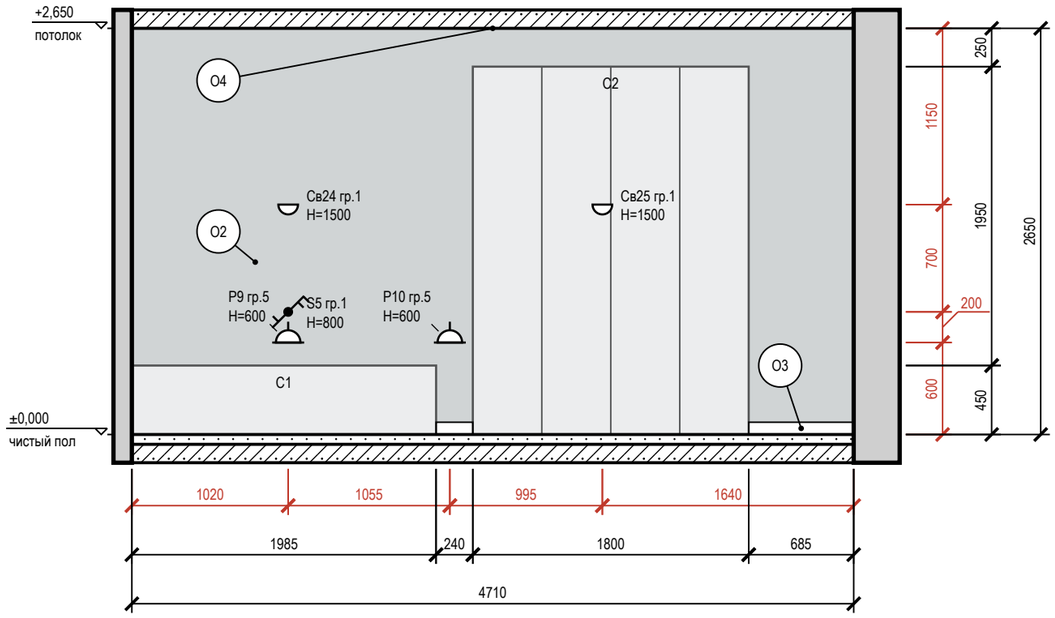

Развёртка стены Б

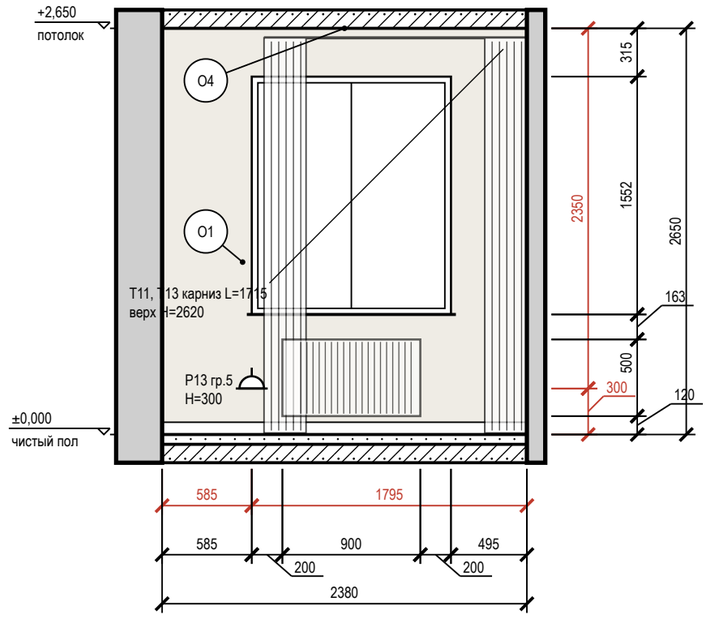

Схема развёрток (М 1:100)

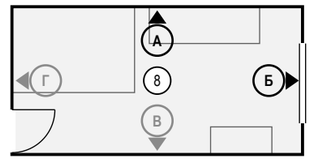

Условные обозначения

- розетка с заземляющим контактом; у знака — марка, ×N постов в рамке, гр. — группа щита, Н — высота оси, мм
- выключатель одноклавишный
- выключатель двухклавишный (флажков — по числу клавиш)
- выключатель с проходной или перекрёстной клавишей (обратный флажок); тип клавиши — в подписи
- светильник настенный (бра), Н — высота оси
- привязки точек и выводов от угла и от пола, мм
- мебель и приборы — фасад по расстановке (условно)
- карниз (шина) и шторы в собранном виде: марка Т, длина L, верх Н
- окно: проём, рама, подоконник
- радиатор отопления; марка — по плану отопления
- стены и перекрытия в сечении
- окраска: тон — цвет по коду производителя (условно)
- О1 — марка отделки по реестру отделки альбома
- А — марка развёртки: буква стены, стрелка — взгляд

Ведомость отделки (на листе)

Марка	Поверхность	Материал, изделие	Цвет, код	Кол.
О1	стены	окраска, Farrow & Ball Modern Emulsion, матовая, подготовка Q3	Farrow & Ball No. 291 «School House White — тёплый меловой белый»	4,3 м²
О2	акцентная стена	окраска, Farrow & Ball Modern Emulsion, матовая, подготовка Q3	Farrow & Ball No. 289 «Inchyra Blue — тёмный сине-серый»	12,5 м²
О3	плинтус	плинтус МДФ, h 80 мм, аналог: плинтус МДФ под покраску 80×16	Farrow & Ball No. 291 «School House White — тёплый меловой белый»	3,3 м
О4	потолок	окраска, Tikkurila Anti-Reflex 2, глубокоматовая, подготовка Q3	NCS S 0502-Y «Белый с лёгкой желтизной»	11,4 м²

Допущения и предложения на листе

Основа листа: размеры сняты со скана обмерного плана KV design (см): часть подписей не читается, помещения выровнены по читаемым размерам; контрольный обмер не выполнен (К-1); высота потолка 2650 мм принята по отметкам обмера (Н = 2,50…2,66 м, ригель 2,28 м) — уточнить при обмере (К-2); толщины стен 300 / 120 мм приняты, межквартирная стена и колонны — по скану, не замерены (К-1); разрешённая мощность 15 кВт принята по типовым ТУ; при объединении двух квартир — переоформление ТУ (К-4).
См. лист открытых вопросов (лист 6, записи К-1, К-2, К-4).

Примечания

1. Развёртки — вид на стену изнутри помещения, по часовой стрелке; расположение — на схеме листа и на листе 65; размеры — в мм по чистовым поверхностям; отметки — в м от ±0,000; высоты Н — от чистого пола помещения до оси изделия, у декора — до центра.
2. Красные цепочки — привязки электроточек и выводов: по горизонтали от угла чистовых стен, по вертикали от чистого пола, до оси изделия; звенья короче 3 мм на листе вынесены во второй ярус (ближняя к стене цепочка).
3. У знака электроточки: марка (Р — розетка, S — выключатель, Св — светильник, ЭВ — вывод кабеля), ×N — число постов в рамке, гр. — группа щита, Н — высота оси от чистого пола, мм; группы по клавишам выключателя — на листе выключателей.
4. Схема мебели, приборов и декора не является технической документацией для производства мебели; габариты — по паспортам изделий.
5. Карнизы (шины) — по ведомости текстиля декоратора; длина L и верх Н — по развёртке, крепление — до окраски потолка.
6. Линии узора (швы плитки, складки штор, рёбра радиаторов) прерываются у знаков и выносок — просвет между линиями не менее 0,7 мм.

1000 мм · печать 1:1

Изм.	Кол.уч	Лист	№ док.	Подп.	Дата
Разраб.		Кырлан А.С.			18.10.26
Пров.					
ГИП					
Н. контр.					
Утв.					

ГД-2026-009-АИ

Квартира 103 м²

Общая площадь 100,72* м² · * размеры со скана, не замерены (реестр — л. 6, К-1)

Дизайн-проект интерьера	Стадия	Лист	Листов
	РП	81	96

Развёртки стен А, Б. Спальня 2 (пом. 8)

М 1:40

Кырлан Александр Сергеевич

выпуск 18.10.2026 № 53dc234b8d · стр. 92 из 135

Развёртки стен В, Г. Спальня 2 (пом. 8)

Спальня 2 (пом. 8) · вид изнутри помещения · размеры в мм, отметки в м

ПРЕДВАРИТЕЛЬНО · не для производства работ · открыто пунктов: 4 (реестр — л. 6)

Развёртка стены В

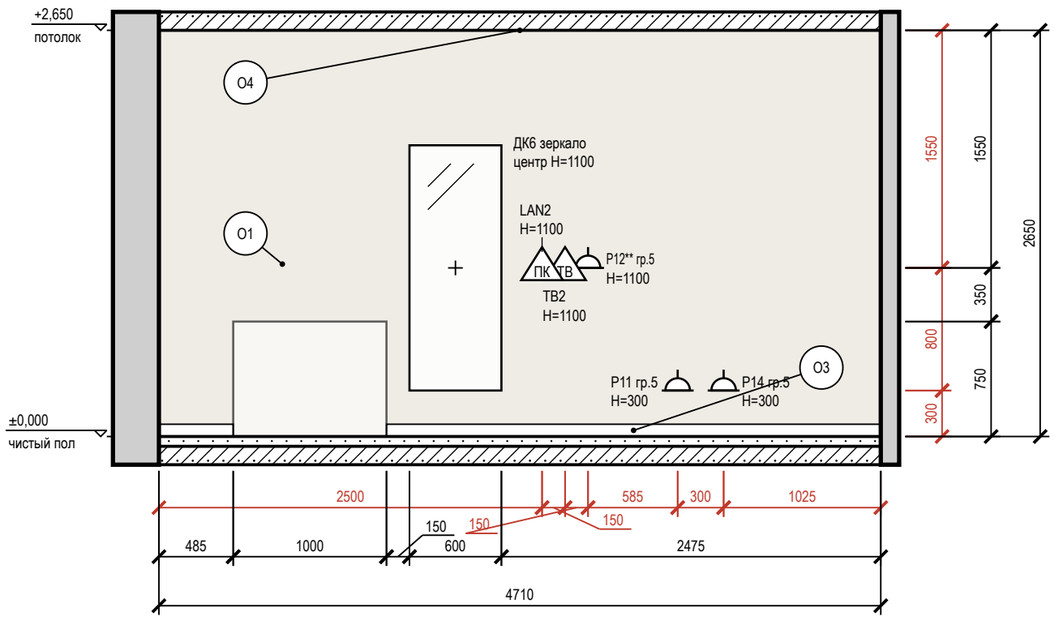

Развёртка стены Г

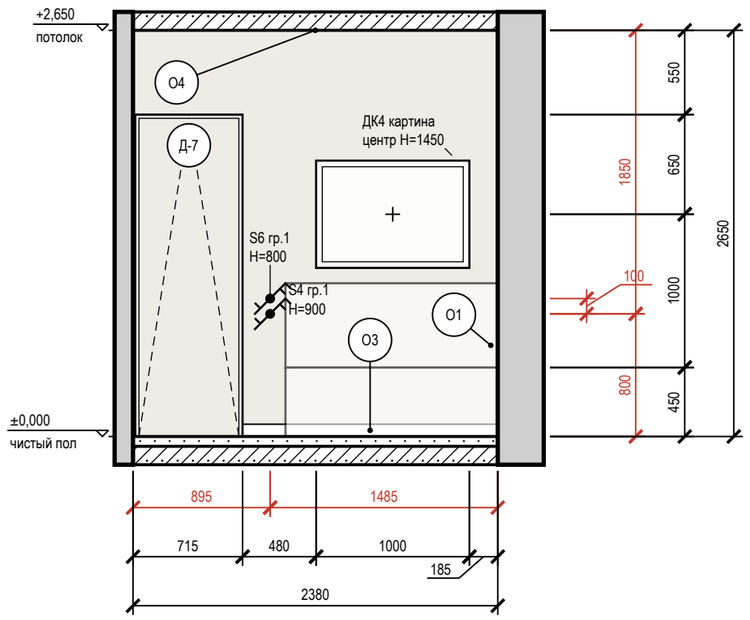

Схема развёрток (М 1:100)

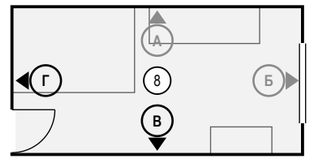

Условные обозначения

- розетка с заземляющим контактом; у знака — марка, ×N постов в рамке, гр. — группа щита, Н — высота оси, мм
- выключатель одноклавишный
- выключатель двухклавишный (флажков — по числу клавиш)
- выключатель с проходной или перекрёстной клавишей (обратный флажок); тип клавиши — в подписи
- ПК — розетка компьютерная RJ45
- ТВ — розетка телевизионная
- привязки точек и выводов от угла и от пола, мм
- мебель и приборы — фасад по расстановке (условно)
- картина (декор): марка Д, крест — центр, Н — высота центра, мм
- зеркало: марка Д, крест — центр, Н — высота центра, мм
- дверь скрытого монтажа: полотно в плоскости стены (узел — на листе узлов)
- стены и перекрытия в сечении
- окраска: тон — цвет по коду производителя (условно)
- О1 — марка отделки по реестру отделки альбома
- А — марка развёртки: буква стены, стрелка — взгляд

Ведомость отделки (на листе)

Марка	Поверхность	Материал, изделие	Цвет, код	Кол.
О1	стены	окраска, Farrow & Ball Modern Emulsion, матовая, подготовка Q3	Farrow & Ball No. 291 «School House White — тёплый меловой белый»	17,3 м²
О3	плинтус	плинтус МДФ, h 80 мм, аналог: плинтус МДФ под покраску 80×16	Farrow & Ball No. 291 «School House White — тёплый меловой белый»	5,4 м
О4	потолок	окраска, Tikkurila Anti-Reflex 2, глубокоматовая, подготовка Q3	NCS S 0502-Y «Белый с лёгкой желтизной»	11,4 м²

Допущения и предложения на листе

Основа листа: размеры сняты со скана обмерного плана KV design (см): часть подписей не читается, помещения выровнены по читаемым размерам; контрольный обмер не выполнен (К-1); высота потолка 2650 мм принята по отметкам обмера (Н = 2,50…2,66 м, ригель 2,28 м) — уточнить при обмере (К-2); толщины стен 300 / 120 мм приняты, межквартирная стена и колонны — по скану, не замерены (К-1); разрешённая мощность 15 кВт принята по типовым ТУ; при объединении двух квартир — переоформление ТУ (К-4).

Знак «**» — предложение проектировщика, заказчиком не утверждено (согласовать с заказчиком): записи в реестре нет: Р12 — высота 1100 мм выше нормы 1 м (ПУЭ 6.6.30) по назначению: питание ТВ над комодом, в одной зоне с выводами ТВ2 и LAN2.

См. лист открытых вопросов (лист 6, записи К-1, К-2, К-4).

Примечания

1. Развёртки — вид на стену изнутри помещения, по часовой стрелке; расположение — на схеме листа и на листе 65; размеры — в мм по чистовым поверхностям; отметки — в м от ±0,000; высоты Н — от чистого пола помещения до оси изделия, у декора — до центра.
2. Красные цепочки — привязки электроточек и выводов: по горизонтали от угла чистовых стен, по вертикали от чистого пола, до оси изделия; звенья короче 3 мм на листе вынесены во второй ярус (ближняя к стене цепочка).
3. У знака электроточки: марка (Р — розетка, S — выключатель, Св — светильник, ЭВ — вывод кабеля), ×N — число постов в рамке, гр. — группа щита, Н — высота оси от чистого пола, мм; группы по клавишам выключателя — на листе выключателей.
4. Схема мебели, приборов и декора не является технической документацией для производства мебели; габариты — по паспортам изделий.
5. Картины и зеркала крепить к основанию по паспорту изделия (закладные и анкеры — в перечне скрытых работ); крест — ось центра предмета.
6. Двери скрытого монтажа — полотно в плоскости стены, отделка стены по полотну, плинтус прерывается у короба (узел — на листе узлов).

1000 мм · печать 1:1

Изм.	Кол.уч	Лист	№ док.	Подп.	Дата
Разраб.		Кырлан А.С.			18.10.26
Пров.					
ГИП					
Н. контр.					
Утв.					

ГД-2026-009-АИ

Квартира 103 м²

Общая площадь 100,72* м² · * размеры со скана, не замерены (реестр — л. 6, К-1)

Дизайн-проект интерьера

Стадия	Лист	Листов
РП	82	96

Развёртки стен В, Г. Спальня 2 (пом. 8)

М 1:40

Кырлан Александр Сергеевич

выпуск 18.10.2026 № 53dc234b8d · стр. 93 из 135

Развёртки стен А, Б, В. Коридор (пом. 9)

Коридор (пом. 9) · вид изнутри помещения · размеры в мм, отметки в м

ПРЕДВАРИТЕЛЬНО · не для производства работ · открыто пунктов: 4 (реестр — л. 6)

Развёртка стены А

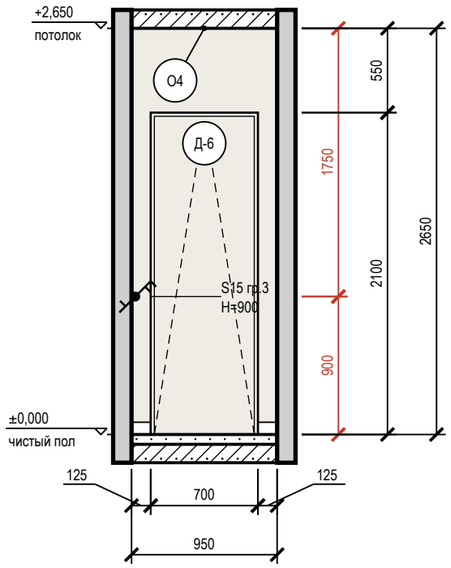

Развёртка стены Б

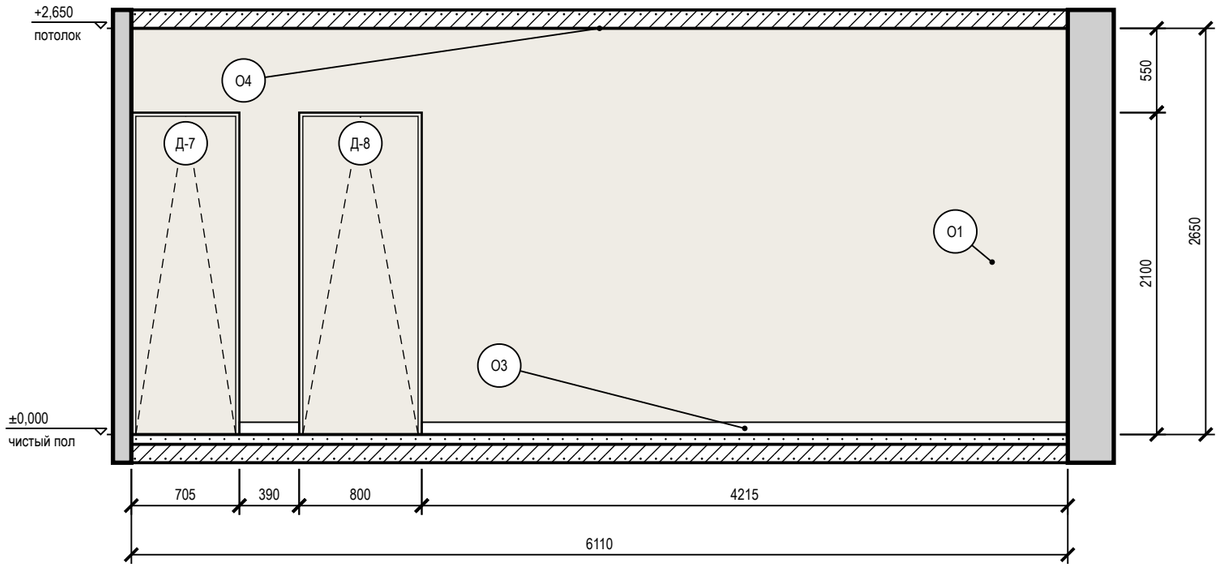

Развёртка стены В

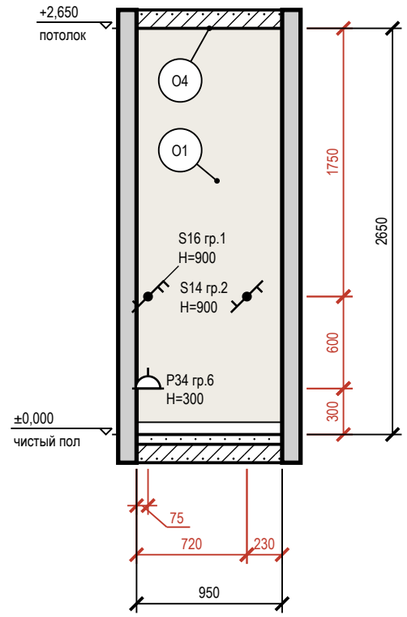

Схема развёрток (М 1:100)

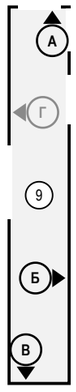

Условные обозначения

- розетка с заземляющим контактом; у знака — марка, ×N постов в рамке, гр. — группа щита, Н — высота оси, мм
- выключатель одноклавишный
- выключатель двухклавишный (флажков — по числу клавиш)
- выключатель с проходной или перекрёстной клавишей (обратный флажок); тип клавиши — в подписи
- привязки точек и выводов от угла и от пола, мм
- мебель и приборы — фасад по расстановке (условно)
- дверь скрытого монтажа: полотно в плоскости стены (узел — на листе узлов)
- стены и перекрытия в сечении
- окраска: тон — цвет по коду производителя (условно)
- О1 — марка отделки по реестру отделки альбома
- А — марка развёртки: буква стены, стрелка — взгляд

Ведомость отделки (на листе)

Марка	Поверхность	Материал, изделие	Цвет, код	Кол.
О1	стены	окраска, Farrow & Ball Modern Emulsion, матовая, подготовка Q3	Farrow & Ball No. 291 «School House White тёплый меловой белый»	16,6 м²
О3	плинтус	плинтус МДФ, h 80 мм, аналог: плинтус МДФ под покраску 80×16	Farrow & Ball No. 291 «School House White тёплый меловой белый»	5,8 м
О4	потолок	окраска, Tikkurila Anti-Reflex 2, глубокоматовая, подготовка Q3	NCS S 0502-Y «Белый с лёгкой желтизной»	6 м²

Допущения и предложения на листе

Основа листа: размеры сняты со скана обмерного плана KV design (см): часть подписей не читается, помещения выровнены по читаемым размерам; контрольный обмер не выполнен (К-1); высота потолка 2650 мм принята по отметкам обмера (Н = 2,50…2,66 м, ригель 2,28 м) — уточнить при обмере (К-2); толщины стен 300 / 120 мм приняты, межквартирная стена и колонны — по скану, не замерены (К-1); разрешённая мощность 15 кВт принята по типовым ТУ; при объединении двух квартир — переоформление ТУ (К-4).
См. лист открытых вопросов (лист 6, записи К-1, К-2, К-4).

Примечания

1. Развёртки — вид на стену изнутри помещения, по часовой стрелке; расположение — на схеме листа и на листе 65; размеры — в мм по чистовым поверхностям; отметки — в м от ±0,000; высоты Н — от чистого пола помещения до оси изделия, у декора — до центра.
2. Красные цепочки — привязки электроточек и выводов: по горизонтали от угла чистовых стен, по вертикали от чистого пола, до оси изделия; звенья короче 3 мм на листе вынесены во второй ярус (ближняя к стене цепочка).
3. У знака электроточки: марка (Р — розетка, S — выключатель, Св — светильник, ЭВ — вывод кабеля), ×N — число постов в рамке, гр. — группа щита, Н — высота оси от чистого пола, мм; группы по клавишам выключателя — на листе выключателей.
4. Схема мебели, приборов и декора не является технической документацией для производства мебели; габариты — по паспортам изделий.
5. Двери скрытого монтажа — полотно в плоскости стены, отделка стены по полотну, плинтус прерывается у короба (узел — на листе узлов).

1000 мм · печать 1:1

Изм.	Кол.уч	Лист	№ док.	Подп.	Дата
Разраб.		Кырлан А.С.			18.10.26
Пров.					
ГИП					
Н. контр.					
Утв.					

ГД-2026-009-АИ

Квартира 103 м²

Общая площадь 100,72* м² · * размеры со скана, не замерены (реестр — л. 6, К-1)

Дизайн-проект интерьера

Стадия	Лист	Листов
РП	83	96

Развёртки стен А, Б, В. Коридор (пом. 9)

М 1:40

Кырлан Александр Сергеевич

выпуск 18.10.2026 № 53dc2346b8d · стр. 94 из 135

Развёртка стены Г. Коридор (пом. 9)

Коридор (пом. 9) · вид изнутри помещения · размеры в мм, отметки в м

ПРЕДВАРИТЕЛЬНО · не для производства работ · открыто пунктов: 4 (реестр — л. 6)

Развёртка стены Г

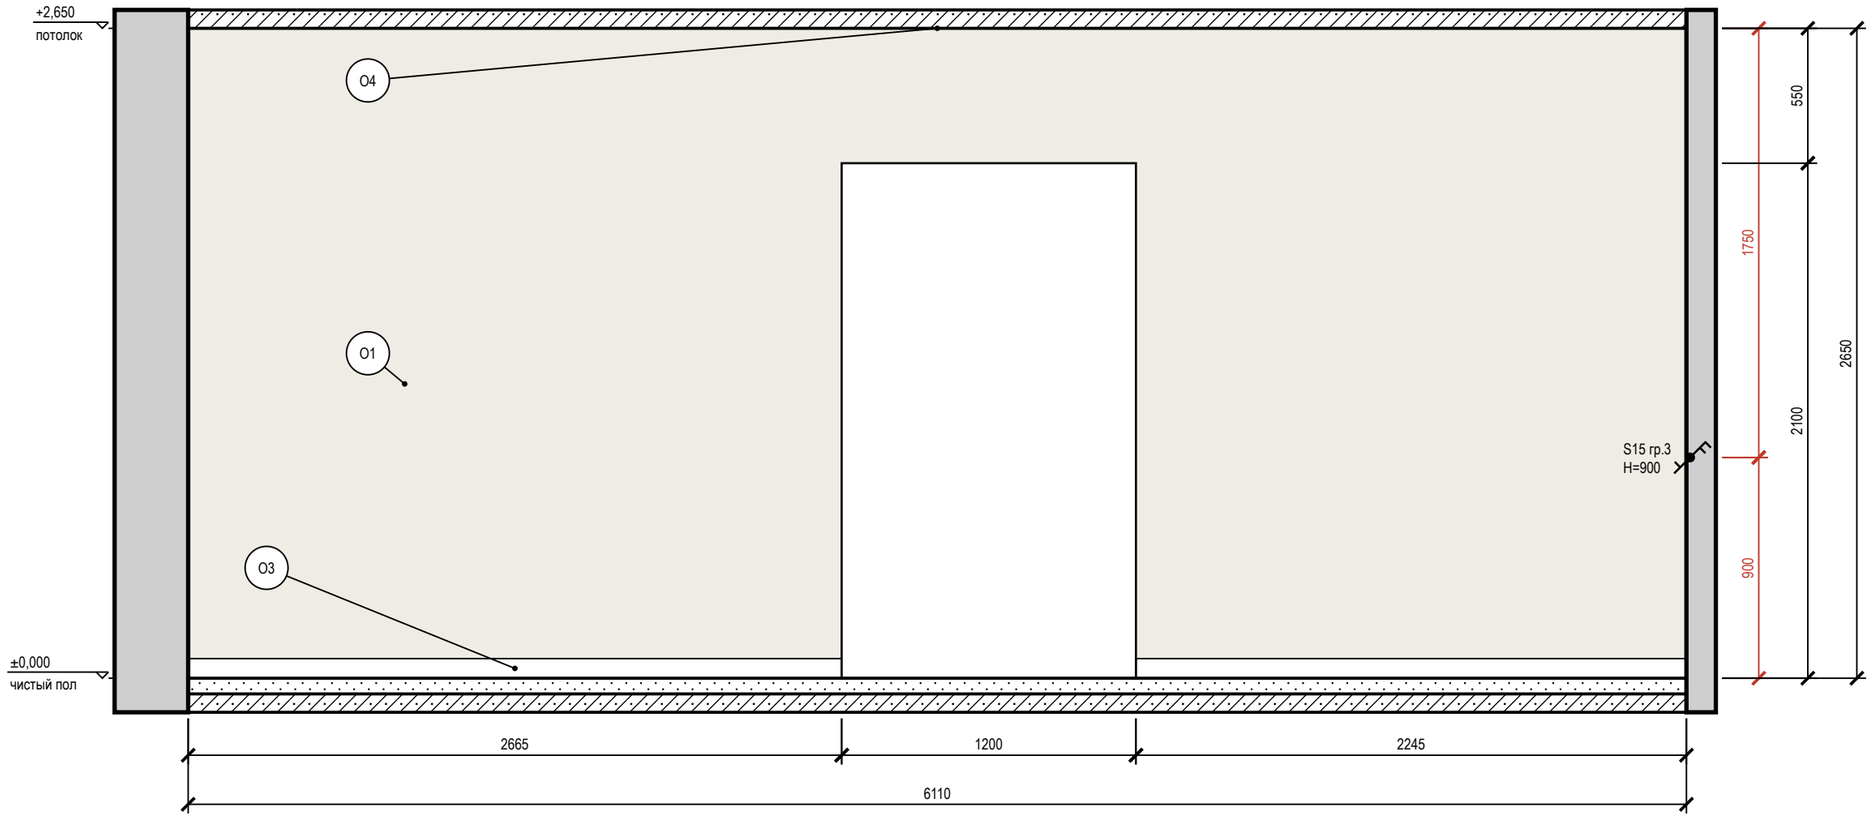

Схема развёрток (М 1:100)

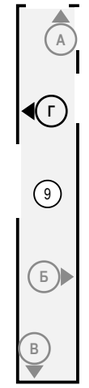

Условные обозначения

- выключатель одноклавишный
- выключатель двухклавишный (флажков — по числу клавиш)
- выключатель с проходной или перекрёстной клавишей (обратный флажок); тип клавиши — в подписи
- привязки точек и выводов от угла и от пола, мм
- мебель и приборы — фасад по расстановке (условно)
- дверной проём; марка двери — в кружке
- стены и перекрытия в сечении
- окраска: тон — цвет по коду производителя (условно)
- О1 — марка отделки по реестру отделки альбома
- А — марка развёртки: буква стены, стрелка — взгляд

Допущения и предложения на листе

Основа листа: размеры сняты со скана обмерного плана KV design (см): часть подписей не читается, помещения выровнены по читаемым размерам; контрольный обмер не выполнен (К-1); высота потолка 2650 мм принята по отметкам обмера (Н = 2,50…2,66 м, ригель 2,28 м) — уточнить при обмере (К-2); толщины стен 300 / 120 мм приняты, межквартирная стена и колонны — по скану, не замерены (К-1); разрешённая мощность 15 кВт принята по типовым ТУ; при объединении двух квартир — переоформление ТУ (К-4).

См. лист открытых вопросов (лист 6, записи К-1, К-2, К-4).

Примечания

1. Развёртки — вид на стену изнутри помещения, по часовой стрелке; расположение — на схеме листа и на листе 65; размеры — в мм по чистовым поверхностям; отметки — в м от ±0,000; высоты Н — от чистого пола помещения до оси изделия, у декора — до центра.
2. Красные цепочки — привязки электроточек и выводов: по горизонтали от угла чистовых стен, по вертикали от чистого пола, до оси изделия; звенья короче 3 мм на листе вынесены во второй ярус (ближняя к стене цепочка).
3. У знака электроточки: марка (Р — розетка, S — выключатель, Св — светильник, ЭВ — вывод кабеля), ×N — число постов в рамке, гр. — группа щита, Н — высота оси от чистого пола, мм; группы по клавишам выключателя — на листе выключателей.
4. Схема мебели, приборов и декора не является технической документацией для производства мебели; габариты — по паспортам изделий.

1000 мм · печать 1:1

Изм.	Кол.уч	Лист	№ док.	Подп.	Дата
Разраб.		Кырлан А.С.			18.10.26
Пров.					
ГИП					
Н. контр.					
Утв.					

ГД-2026-009-АИ

Квартира 103 м²

Общая площадь 100,72* м² · * размеры со скана, не замерены (реестр — л. 6, К-1)

Дизайн-проект интерьера

Стадия	Лист	Листов
РП	84	96

Развёртка стены Г. Коридор (пом. 9)

М 1:25

Кырлан Александр Сергеевич

выпуск 18.10.2026 № 53dc2348d8d · стр. 95 из 135

Развёртки стен А, Б. Спальня мастер (пом. 10)

Спальня мастер (пом. 10) · вид изнутри помещения · размеры в мм, отметки в м

ПРЕДВАРИТЕЛЬНО · не для производства работ · открыто пунктов: 4 (реестр — л. 6)

Развёртка стены А

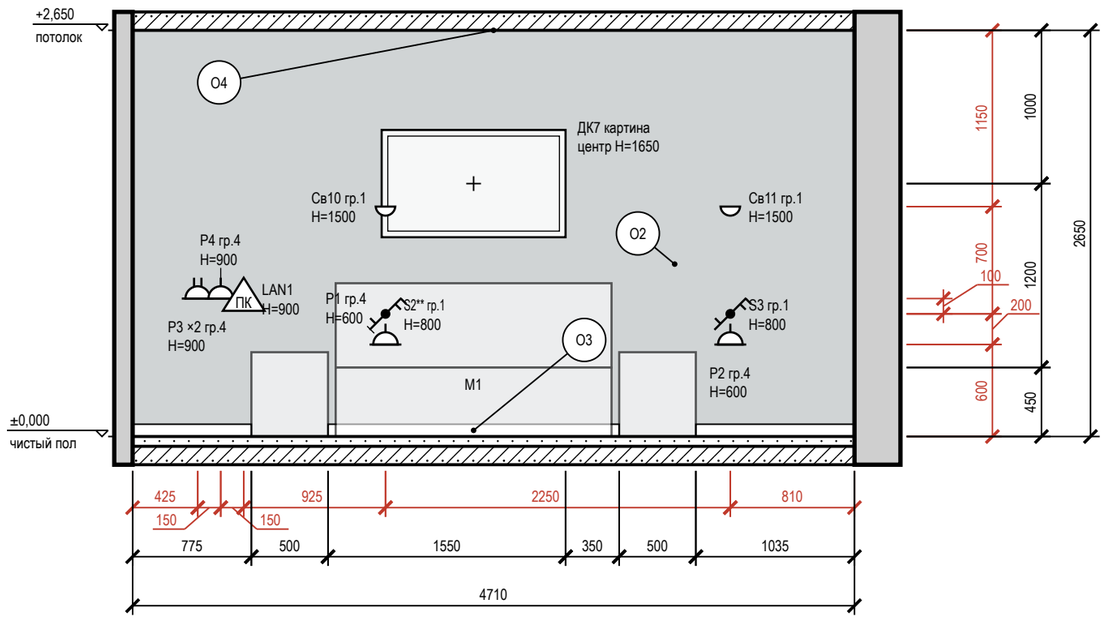

Развёртка стены Б

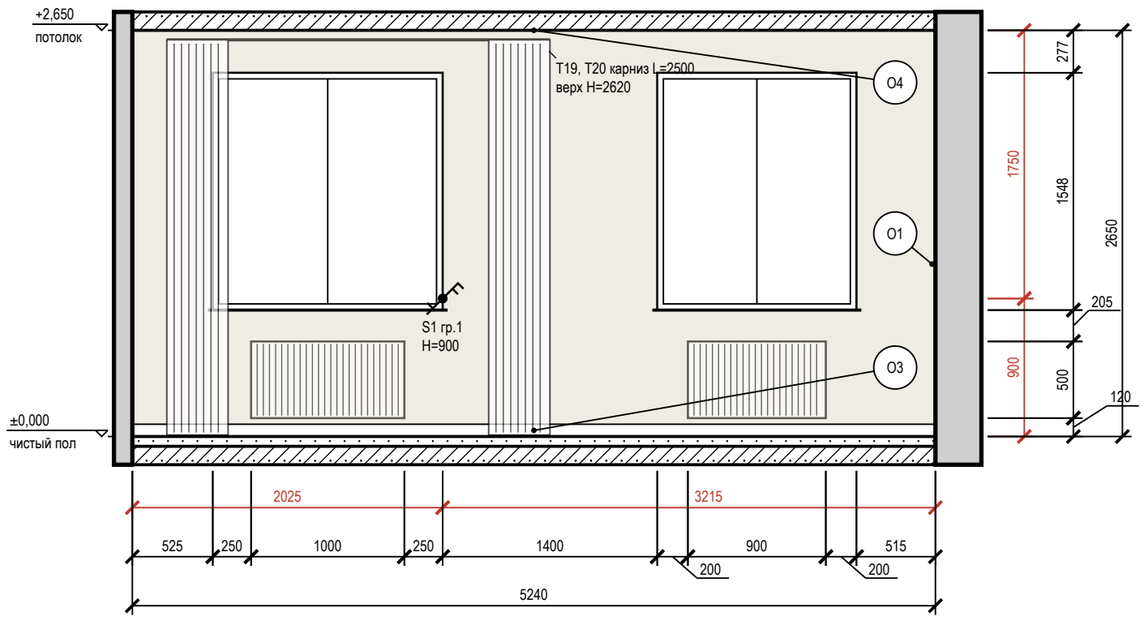

Схема развёрток (М 1:100)

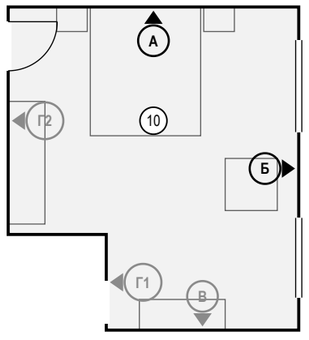

Условные обозначения

- розетка с заземляющим контактом; у знака — марка, ×N постов в рамке, гр. — группа щита, Н — высота оси, мм
- выключатель одноклавишный
- выключатель двухклавишный (флажков — по числу клавиш)
- выключатель с проходной или перекрёстной клавишей (обратный флажок); тип клавиши — в подписи
- светильник настенный (бра), Н — высота оси
- ПК — розетка компьютерная RJ45
- привязки точек и выводов от угла и от пола, мм
- мебель и приборы — фасад по расстановке (условно)
- картина (декор): марка Д, крест — центр, Н — высота центра, мм
- карниз (шина) и шторы в собранном виде: марка Т, длина L, верх Н
- окно: проём, рама, подоконник
- радиатор отопления; марка — по плану отопления
- стены и перекрытия в сечении
- окраска: тон — цвет по коду производителя (условно)
- О1 — марка отделки по реестру отделки альбома
- А — марка развёртки: буква стены, стрелка — взгляд

Ведомость отделки (на листе)

Марка	Поверхность	Материал, изделие	Цвет, код	Кол.
О1	стены	окраска, Farrow & Ball Modern Emulsion, матовая, подготовка Q3	Farrow & Ball No. 291 «School House White — тёплый меловой белый»	9,6 м²
О2	акцентная стена	окраска, Farrow & Ball Modern Emulsion, матовая, подготовка Q3	Farrow & Ball No. 289 «Inchyra Blue — тёмный сине-серый»	12,5 м²
О3	плинтус	плинтус МДФ, h 80 мм, аналог: плинтус МДФ под покраску 80×16	Farrow & Ball No. 291 «School House White — тёплый меловой белый»	8,9 м
О4	потолок	окраска, Tikkurila Anti-Reflex 2, глубокоматовая, подготовка Q3	NCS S 0502-Y «Белый с лёгкой желтизной»	22,5 м²

Допущения и предложения на листе

Основа листа: размеры сняты со скана обмерного плана KV design (см): часть подписей не читается, помещения выровнены по читаемым размерам; контрольный обмер не выполнен (К-1); высота потолка 2650 мм принята по отметкам обмера (Н = 2,50…2,66 м, ригель 2,28 м) — уточнить при обмере (К-2); толщины стен 300 / 120 мм приняты, межквартирная стена и колонны — по скану, не замерены (К-1); разрешённая мощность 15 кВт принята по типовым ТУ; при объединении двух квартир — переоформление ТУ (К-4).

Знак «**» — предложение проектировщика, заказчиком не утверждено (согласовать с заказчиком): записи в реестре нет: S2 — светорегулятор добавлен под диммируемую ленту L3; уровни сценариев выбраны конвейером.

См. лист открытых вопросов (лист 6, записи К-1, К-2, К-4).

Примечания

1. Развёртки — вид на стену изнутри помещения, по часовой стрелке; расположение — на схеме листа и на листе 65; размеры — в мм по чистовым поверхностям; отметки — в м от ±0,000; высоты Н — от чистого пола помещения до оси изделия, у декора — до центра.
2. Красные цепочки — привязки электроточек и выводов: по горизонтали от угла чистовых стен, по вертикали от чистого пола, до оси изделия; звенья короче 3 мм на листе вынесены во второй ярус (ближняя к стене цепочка).
3. У знака электроточки: марка (Р — розетка, S — выключатель, Св — светильник, ЭВ — вывод кабеля), ×N — число постов в рамке, гр. — группа щита, Н — высота оси от чистого пола, мм; группы по клавишам выключателя — на листе выключателей.
4. Схема мебели, приборов и декора не является технической документацией для производства мебели; габариты — по паспортам изделий.
5. Картины и зеркала крепить к основанию по паспорту изделия (закладные и анкеры — в перечне скрытых работ); крест — ось центра предмета.
6. Карнизы (шины) — по ведомости текстиля декоратора; длина L и верх Н — по развёртке, крепление — до окраски потолка.

1000 мм · печать 1:1

Изм.	Кол.уч	Лист	№ док.	Подп.	Дата
Разраб.		Кырлан А.С.			18.10.26
Пров.					
ГИП					
Н. контр.					
Утв.					

ГД-2026-009-АИ

Квартира 103 м²

Общая площадь 100,72* м² · * размеры со скана, не замерены (реестр — л. 6, К-1)

Дизайн-проект интерьера

Стадия	Лист	Листов
РП	85	96

Развёртки стен А, Б. Спальня мастер (пом. 10)

М 1:40

Кырлан Александр Сергеевич

выпуск 18.10.2026 № 53dc234b8d · стр. 96 из 135

Развёртки стен В, Г1, Г2. Спальня мастер (пом. 10)

Спальня мастер (пом. 10) · вид изнутри помещения · размеры в мм, отметки в м

ПРЕДВАРИТЕЛЬНО · не для производства работ · открыто пунктов: 4 (реестр — л. 6)

Развёртка стены В

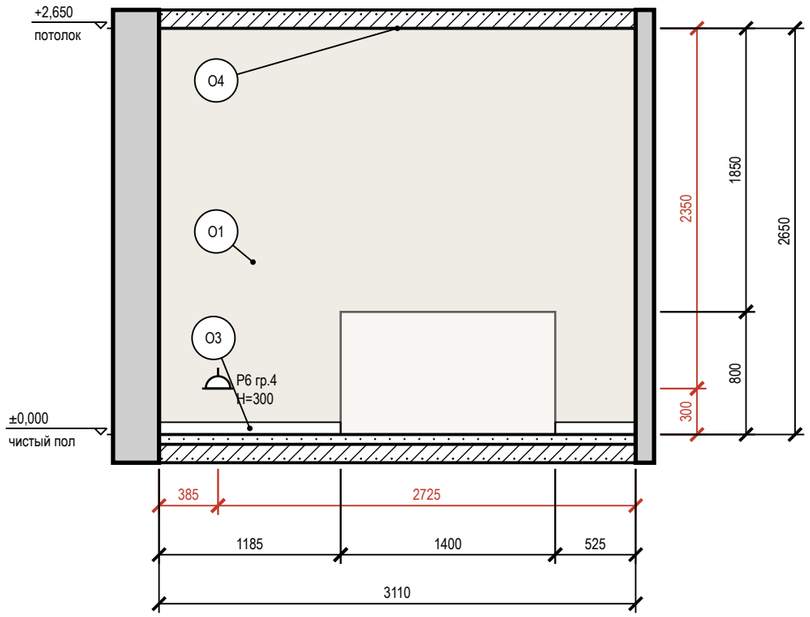

Развёртка стены Г1

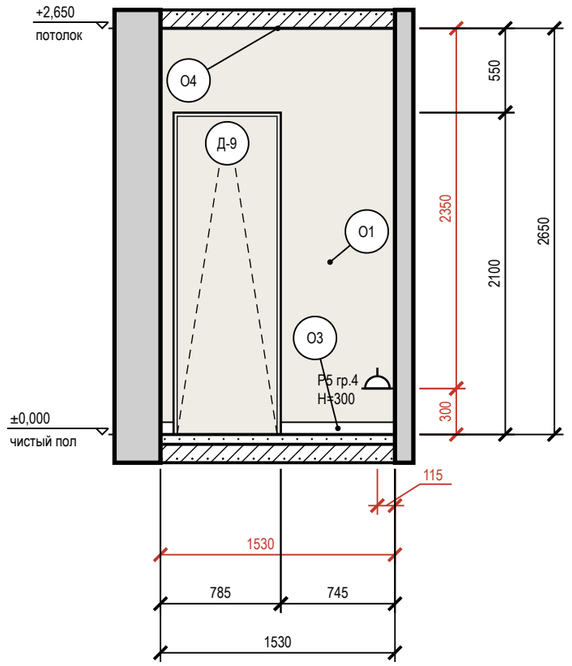

Развёртка стены Г2

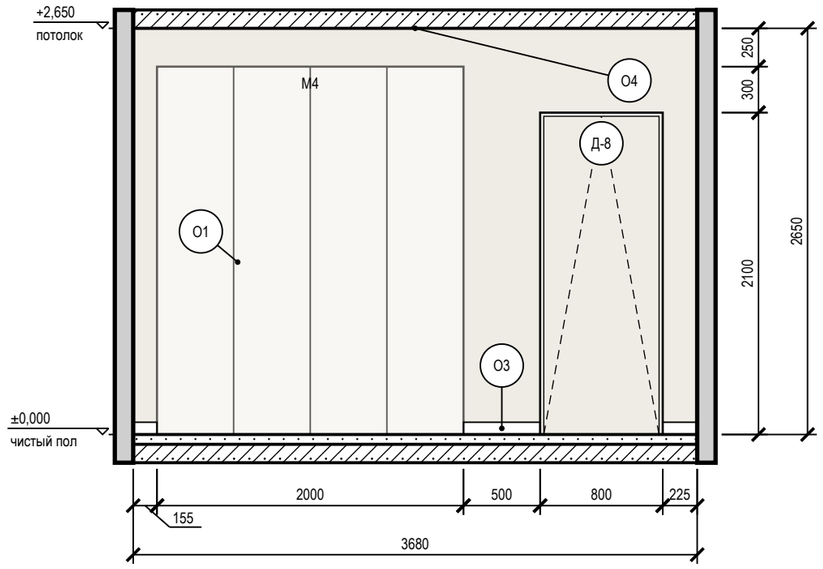

Схема развёрток (М 1:100)

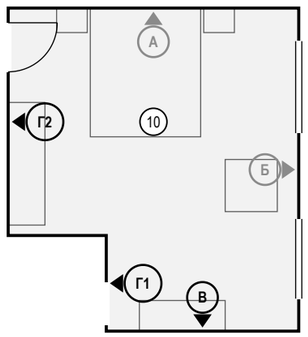

Условные обозначения

- розетка с заземляющим контактом; у знака — марка, ×N постов в рамке, гр. — группа щита, Н — высота оси, мм
- привязки точек и выводов от угла и от пола, мм
- мебель и приборы — фасад по расстановке (условно)
- дверь скрытого монтажа: полотно в плоскости стены (узел — на листе узлов)
- стены и перекрытия в сечении
- окраска: тон — цвет по коду производителя (условно)
- О1 — марка отделки по реестру отделки альбома
- А — марка развёртки: буква стены, стрелка — взгляд

Ведомость отделки (на листе)

Марка	Поверхность	Материал, изделие	Цвет, код	Кол.
О1	стены	окраска, Farrow & Ball Modern Emulsion, матовая, подготовка Q3	Farrow & Ball No. 291 «School House White тёплый меловой белый»	18,9 м²
О3	плинтус	плинтус МДФ, h 80 мм, аналог: плинтус МДФ под покраску 80×16	Farrow & Ball No. 291 «School House White тёплый меловой белый»	3,4 м
О4	потолок	окраска, Tikkurila Anti-Reflex 2, глубокоматовая, подготовка Q3	NCS S 0502-Y «Белый с лёгкой желтизной»	22,5 м²

Допущения и предложения на листе

Основа листа: размеры сняты со скана обмерного плана KV design (см): часть подписей не читается, помещения выровнены по читаемым размерам; контрольный обмер не выполнен (К-1); высота потолка 2650 мм принята по отметкам обмера (Н = 2,50…2,66 м, ригель 2,28 м) — уточнить при обмере (К-2); толщины стен 300 / 120 мм приняты, межквартирная стена и колонны — по скану, не замерены (К-1); разрешённая мощность 15 кВт принята по типовым ТУ; при объединении двух квартир — переоформление ТУ (К-4).

См. лист открытых вопросов (лист 6, записи К-1, К-2, К-4).

Примечания

1. Развёртки — вид на стену изнутри помещения, по часовой стрелке; расположение — на схеме листа и на листе 65; размеры — в мм по чистовым поверхностям; отметки — в м от ±0,000; высоты Н — от чистого пола помещения до оси изделия, у декора — до центра.
2. Красные цепочки — привязки электроточек и выводов: по горизонтали от угла чистовых стен, по вертикали от чистого пола, до оси изделия; звенья короче 3 мм на листе вынесены во второй ярус (ближняя к стене цепочка).
3. У знака электроточки: марка (Р — розетка, S — выключатель, Св — светильник, ЭВ — вывод кабеля), ×N — число постов в рамке, гр. — группа щита, Н — высота оси от чистого пола, мм; группы по клавишам выключателя — на листе выключателей.
4. Схема мебели, приборов и декора не является технической документацией для производства мебели; габариты — по паспортам изделий.
5. Двери скрытого монтажа — полотно в плоскости стены, отделка стены по полотну, плинтус прерывается у короба (узел — на листе узлов).

1000 мм · печать 1:1

Изм.	Кол.уч	Лист	№ док.	Подп.	Дата
Разраб.		Кырлан А.С.			18.10.26
Пров.					
ГИП					
Н. контр.					
Утв.					

ГД-2026-009-АИ

Квартира 103 м²

Общая площадь 100,72* м² · * размеры со скана, не замерены (реестр — л. 6, К-1)

Дизайн-проект интерьера

Стадия	Лист	Листов
РП	86	96

Развёртки стен В, Г1, Г2. Спальня мастер (пом. 10)

М 1:40

Кырлан Александр Сергеевич

выпуск 18.10.2026 № 53dc2348d8d · стр. 97 из 135

Развёртки стен А, Б. Ванная мастер (пом. 11)

Ванная мастер (пом. 11) · вид изнутри помещения · размеры в мм, отметки в м

ПРЕДВАРИТЕЛЬНО · не для производства работ · открыто пунктов: 4 (реестр — л. 6)

Развёртка стены А

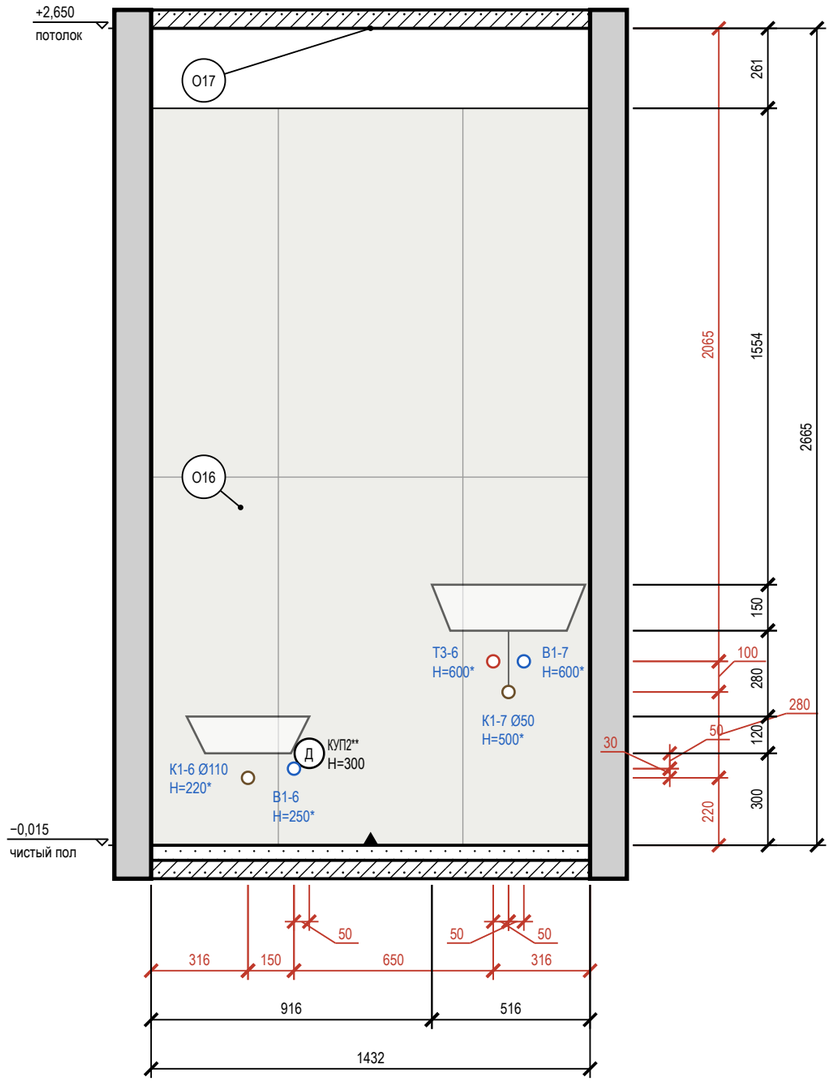

Развёртка стены Б

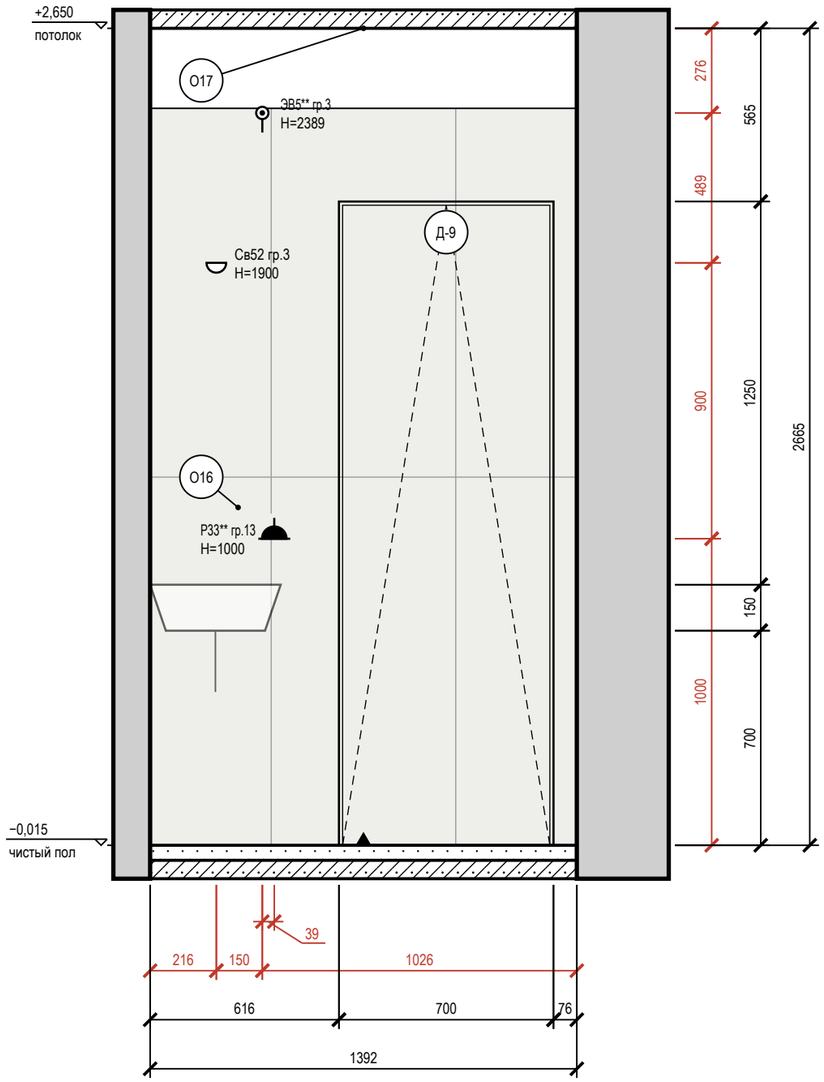

Схема развёрток (М 1:100)

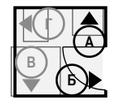

Условные обозначения

- розетка влагозащищённая IP44
- вывод кабеля для подключения прибора (без розетки), марка ЭВ
- светильник настенный (бра), H — высота оси
- вывод В1 (код — в ведомости привязок)
- вывод Т3 (код — в ведомости привязок)
- вывод К1 (код — в ведомости привязок)
- привязки точек и выводов от угла и от пола, мм
- мебель и приборы — фасад по расстановке (условно)
- дверь скрытого монтажа: полотно в плоскости стены (узел — на листе узлов)
- стены и перекрытия в сечении
- плитка: сетка швов по формату, ▲ — ось старта
- О1 — марка отделки по реестру отделки альбома
- А — марка развёртки: буква стены, стрелка — взгляд

Допущения и предложения на листе

Основа листа: размеры сняты со скана обмерного плана KV design (см): часть подписей не читается, помещения выровнены по читаемым размерам; контрольный обмер не выполнен (К-1); высота потолка 2650 мм принята по отметкам обмера (H = 2,50…2,66 м, ригель 2,28 м) — уточнить при обмере (К-2); толщины стен 300 / 120 мм приняты, межквартирная стена и колонны — по скану, не замерены (К-1); разрешённая мощность 15 кВт принята по типовым ТУ; при объединении двух квартир — переоформление ТУ (К-4).

Знак «**» — предложение проектировщика, заказчиком не утверждено (согласовать с заказчиком): записи в реестре нет: Р33 — по образцу: Розетка Р33 на высоте 1100 мм, вне шва плитки; ЭВ5, КУП2 — по образцу: Добавлены выводы к вентиляторам: ЭВ4 (ВР1, ванная) и ЭВ5 (ВР3, санузел 2) — группа 3, высота 2389 мм, включение с основным светом, таймер выбега в вентиляторе; и коробки уравнивания потенциалов КУП1 (ванная) и КУП2 (санузел 2) — высота 300 мм, у входа, вне зон 0–2, проводник от шины PE щита ЩК, сече.

См. лист открытых вопросов (лист 6, записи К-1, К-2, К-4).

Примечания

1. Развёртки — вид на стену изнутри помещения, по часовой стрелке; расположение — на схеме листа и на листе 65; размеры — в мм по чистовым поверхностям; отметки — в м от ±0,000; высоты H — от чистого пола помещения до оси изделия, у декора — до центра.
2. Красные цепочки — привязки электроточек и выводов: по горизонтали от угла чистовых стен, по вертикали от чистого пола, до оси изделия; звенья короче 3 мм на листе вынесены во второй ярус (ближняя к стене цепочка).
3. У знака электроточки: марка (Р — розетка, S — выключатель, Св — светильник, ЭВ — вывод кабеля), ×N — число постов в рамке, гр. — группа щита, H — высота оси от чистого пола, мм; группы по клавишам выключателя — на листе выключателей.
4. Схема мебели, приборов и декора не является технической документацией для производства мебели; габариты — по паспортам изделий (* — высота не задана в проекте, показана по типовому изделию).
5. Выводы ВК — коды и высоты по листу выводов сантехники; * — высота принята по типовой практике монтажа, окончательно — по паспорту прибора.
6. Облицовка — по сетке швов 2 мм, раскладка от оси стены (треугольник у пола), целые ряды от пола; подрезки — по листу раскладки плитки.
7. Гидроизоляция в 2 слоя, заход на стены 200 мм — до облицовки, с актом скрытых работ и тестом проливом (узел — на листе узлов).
8. Двери скрытого монтажа — полотно в плоскости стены, отделка стены по полотну, плинтус прерывается у короба (узел — на листе узлов).
9. Линии узора (швы плитки, складки штор, рёбра радиаторов) прерываются у знаков и выносок — просвет между линиями не менее 0,7 мм.

1000 мм · печать 1:1

Изм.	Кол.уч	Лист	№ док.	Подп.	Дата
Разраб.		Кырлан А.С.			18.10.26
Пров.					
ГИП					
Н. контр.					
Утв.					

ГД-2026-009-АИ

Квартира 103 м²

Общая площадь 100,72* м² · * размеры со скана, не замерены (реестр — л. 6, К-1)

Дизайн-проект интерьера	Стадия	Лист	Листов
	РП	87	96

Развёртки стен А, Б. Ванная мастер (пом. 11)

М 1:20

Кырлан Александр Сергеевич

выпуск 18.10.2026 № 53dc234b8d · стр. 98 из 135

Развёртки стен В, Г. Ванная мастер (пом. 11)

Ванная мастер (пом. 11) · вид изнутри помещения · размеры в мм, отметки в м

ПРЕДВАРИТЕЛЬНО · не для производства работ · открыто пунктов: 4 (реестр — л. 6)

Развёртка стены В

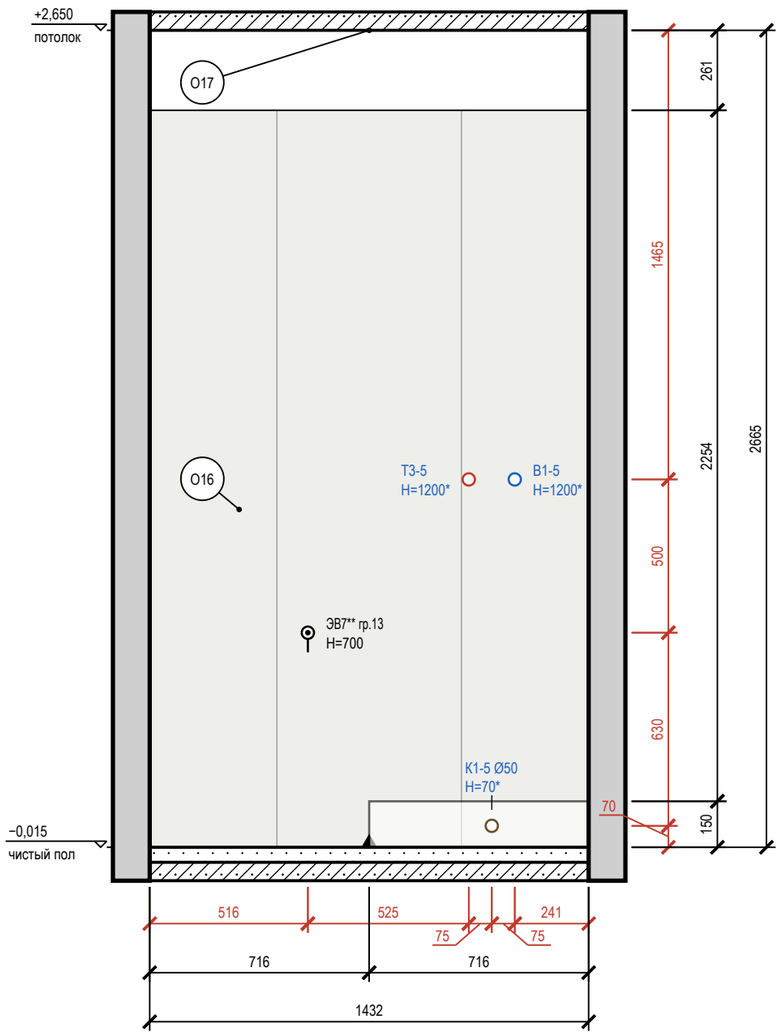

Развёртка стены Г

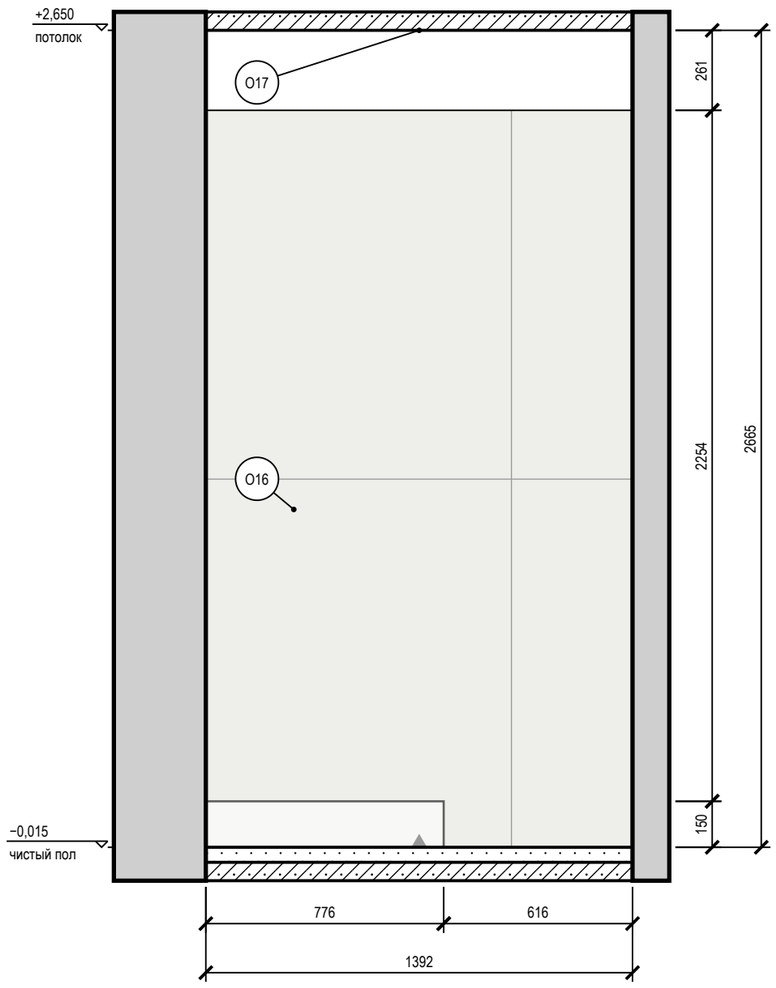

Схема развёрток (М 1:100)

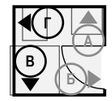

Условные обозначения

- вывод кабеля для подключения прибора (без розетки), марка ЭВ
- вывод В1 (код — в ведомости привязок)
- вывод Т3 (код — в ведомости привязок)
- вывод К1 (код — в ведомости привязок)
- привязки точек и выводов от угла и от пола, мм
- мебель и приборы — фасад по расстановке (условно)
- стены и перекрытия в сечении
- плитка: сетка швов по формату, ▲ — ось старта
- О1 — марка отделки по реестру отделки альбома
- А — марка развёртки: буква стены, стрелка — взгляд

Ведомость отделки (на листе)

Марка	Поверхность	Материал, изделие	Цвет, код	Кол.
О16	стены	облицовка плиткой, Atlas Concorde Marvel Travertine, 600×1200×9 мм, A8UZ, затирка CG2WA	Atlas Concorde A8UZ «Marvel Travertine»	6,8 м²
О17	потолок	окраска, Tikkurila Luja 7, матовая, подготовка Q3	NCS S 0502-Y «Белый с лёгкой желтизной»	2,1 м²

Допущения и предложения на листе

Основа листа: размеры сняты со скана обмерного плана KV design (см): часть подписей не читается, помещения выровнены по читаемым размерам; контрольный обмер не выполнен (К-1); высота потолка 2650 мм принята по отметкам обмера (Н = 2,50…2,66 м, ригель 2,28 м) — уточнить при обмере (К-2); толщины стен 300 / 120 мм приняты, межквартирная стена и колонны — по скану, не замерены (К-1); разрешённая мощность 15 кВт принята по типовым ТУ; при объединении двух квартир — переоформление ТУ (К-4).

Знак «**» — предложение проектировщика, заказчиком не утверждено (согласовать с заказчиком): записи в реестре нет: ЭВ7 — по образцу: Добавлены электрические полотенцесушители IP44: П10 в ванной (480 мм, низ 900 мм) и П13 в санузле 2 (400 мм, низ 900 мм), выводы ЭВ6 и ЭВ7; мощность группы 13 — 2,4 кВт вместо 1,8 кВт.

См. лист открытых вопросов (лист 6, записи К-1, К-2, К-4).

Примечания

1. Развёртки — вид на стену изнутри помещения, по часовой стрелке; расположение — на схеме листа и на листе 65; размеры — в мм по чистовым поверхностям; отметки — в м от ±0,000; высоты Н — от чистого пола помещения до оси изделия, у декора — до центра.
2. Красные цепочки — привязки электроточек и выводов: по горизонтали от угла чистовых стен, по вертикали от чистого пола, до оси изделия; звенья короче 3 мм на листе вынесены во второй ярус (ближняя к стене цепочка).
3. У знака электроточки: марка (Р — розетка, S — выключатель, Св — светильник, ЭВ — вывод кабеля), ×N — число постов в рамке, гр. — группа щита, Н — высота оси от чистого пола, мм; группы по клавишам выключателя — на листе выключателей.
4. Схема мебели, приборов и декора не является технической документацией для производства мебели; габариты — по паспортам изделий (* — высота не задана в проекте, показана по типовому изделию).
5. Выводы ВК — коды и высоты по листу выводов сантехники; * — высота принята по типовой практике монтажа, окончательно — по паспорту прибора.
6. Облицовка — по сетке швов 2 мм, раскладка от оси стены (треугольник у пола), целые ряды от пола; подрезки — по листу раскладки плитки.
7. Гидроизоляция в 2 слоя, заход на стены 200 мм — до облицовки, с актом скрытых работ и тестом проливом (узел — на листе узлов).

1000 мм · печать 1:1

Изм.	Кол.уч	Лист	№ док.	Подп.	Дата
Разраб.		Кырлан А.С.			18.10.26
Пров.					
ГИП					
Н. контр.					
Утв.					

ГД-2026-009-АИ

Квартира 103 м²

Общая площадь 100,72* м² · * размеры со скана, не замерены (реестр — л. 6, К-1)

Дизайн-проект интерьера

Стадия	Лист	Листов
РП	88	96

Развёртки стен В, Г. Ванная мастер (пом. 11)

М 1:20

Кырлан Александр Сергеевич

выпуск 18.10.2026 № 53dc234b8d · стр. 99 из 135

Узлы

Пороги и стыки покрытий, скрытые двери, короба стояков, гидроизоляция, плинтус

1 Порог 15 мм: мокрая зона — жилое помещение (М 1:10)

Применение: двери Д-5, Д-9; места — лист 65

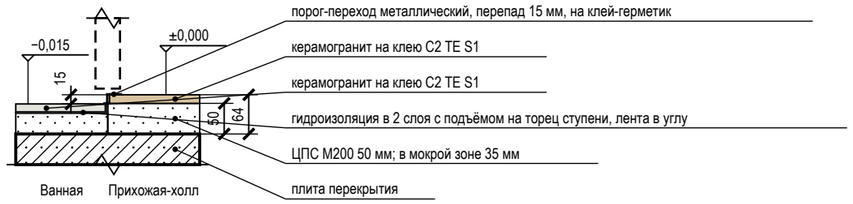

2 Дверь скрытого монтажа в плоскости стены, плинтус (М 1:5)

Применение: двери Д-2, Д-3, Д-4, Д-5, Д-6, Д-7, Д-8, Д-9; места — лист 65

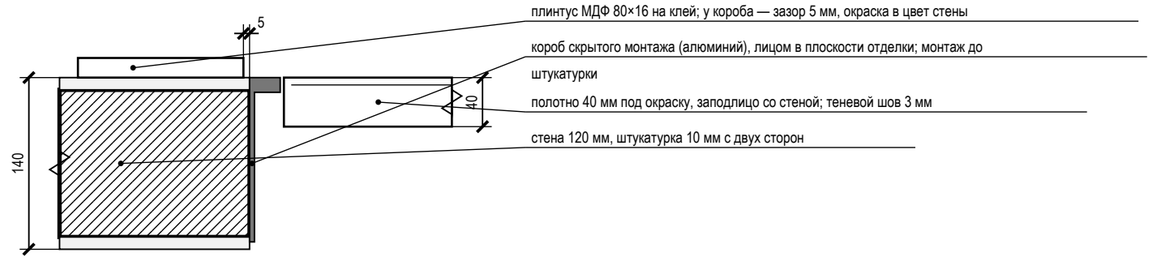

3 Короб стояков К1-1, К1-2 (кухня) с люком и звукоизоляцией (М 1:10)

Применение: пом. 6, 5, 11, 7; места — лист 65

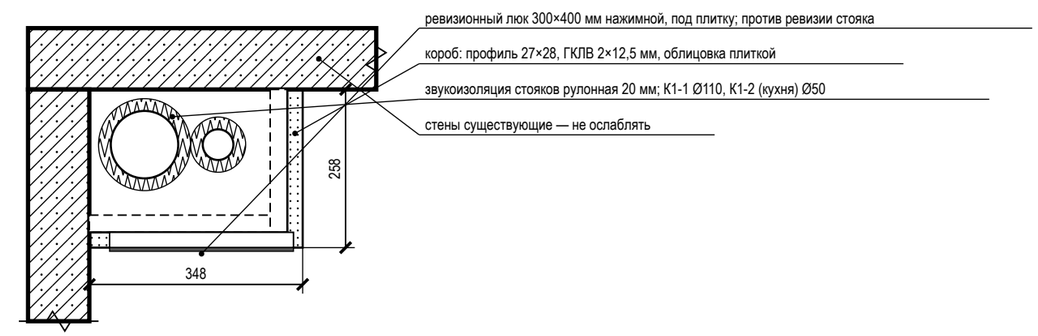

4 Гидроизоляция санузла: заход на стены 200 мм, примыкание ванны (М 1:20)

Применение: пом. 6, 11; места — лист 65

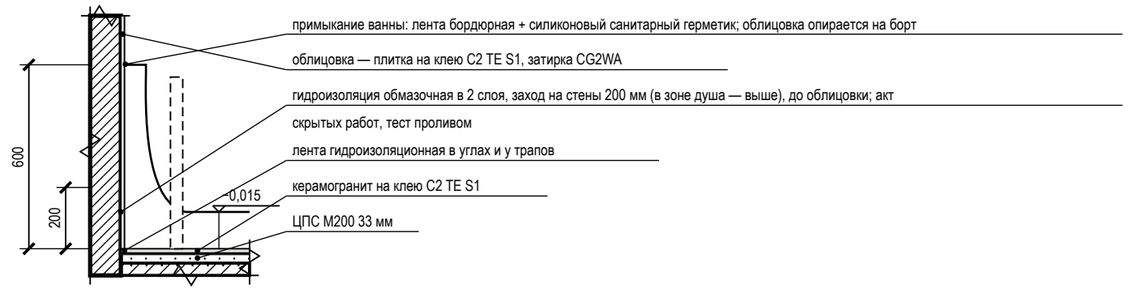

5 Плинтус МДФ 80×16 мм у окрашенной стены (М 1:10)

Применение: пом. 1, 2, 3, 4, 5, 7, 8, 9, 10; места — лист 65

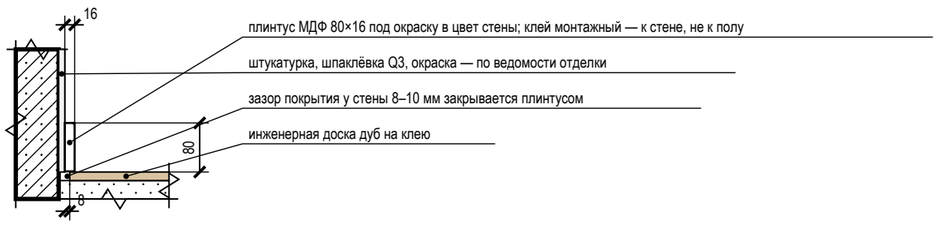

Условные обозначения

- железобетон (плита, стены)
- кладка, перегородка
- стяжка, раствор
- гипсокартон ГКЛВ
- звукоизоляция, эластичный заполнитель
- плитка, керамогранит на клею
- инженерная доска (покрытие пола)
- металлический профиль (порог, Т-профиль, короб двери)
- гидроизоляция (обмазочная, лента)

Примечания

1. Узлы — типовые решения проекта для мест, отмеченных выносками на листе схемы расположения развёрток и узлов; размеры — в мм, отметки — в м от ±0,000.
2. Узлы с гидроизоляцией, закладными и коробами скрытого монтажа принимаются по актам скрытых работ до закрытия отделкой; гидроизоляция — после теста проливом (24 ч).
3. Марки изделий (порог, Т-профиль, короб скрытой двери, люк) — по спецификациям; замена — на аналог с теми же габаритами по согласованию с автором проекта.

Допущения и предложения на листе

Основа листа: размеры сняты со скана обмерного плана KV design (см): часть подписей не читается, помещения выровнены по читаемым размерам; контрольный обмер не выполнен (К-1); высота потолка 2650 мм принята по отметкам обмера (Н = 2,50…2,66 м, ригель 2,28 м) — уточнить при обмере (К-2); толщины стен 300 / 120 мм приняты, межквартирная стена и колонны — по скану, не замерены (К-1); разрешённая мощность 15 кВт принята по типовым ТУ; при объединении двух квартир — переоформление ТУ (К-4).
См. лист открытых вопросов (лист 6, записи К-1, К-2, К-4).

Изм.	Кол.уч	Лист	№ док.	Подп.	Дата
Разраб.		Кырлан А.С.			18.10.26
Пров.					
ГИП					
Н. контр.					
Утв.					

ГД-2026-009-АИ

Квартира 103 м²

Общая площадь 100,72* м² · * размеры со скана, не замерены (реестр — л. 6, К-1)

Дизайн-проект интерьера

Стадия	Лист	Листов
РП	89	96

Узлы

М б/м

Кырлан Александр Сергеевич

выпуск 18.10.2026 № 53dc234b8d · стр. 100 из 135

10

Смета

Кырлан Александр Сергеевич

выпуск 18.10.2026 № 53dc234b8d · стр. 101 из 135

Ведомость объёмов работ

ПРЕДВАРИТЕЛЬНО · не для производства работ · открыто пунктов: 4 (реестр — л. 6)

Объёмы по помещениям от чертежа · площади в м², длины в м · формула, правило проёмов и источник в каждой строке

Ведомость объёмов работ по помещениям

Поз.	Наименование работ (материал, число слоёв)	Ед. изм.	Объём по помещениям (№ по экспликации)											Всего	Формула подсчёта	Правило проёмов	Источник	Цена за ед., ₽	Стоимость, ₽
			1	2	3	4	5	6	7	8	9	10	11						
1. Демонтаж и черновые работы																			
1	Демонтаж существующего покрытия пола до основания	м²	10,57	2,93	20,32	12,91	6,52	3,91	1,51	11,42	6,02	22,48	2,13	100,72	S пом.		л. 12, 13	по КП	
2	Демонтаж существующей отделки стен до основания	м²	32,70	17,61	37,18	35,51	23,54	20,12	11,89	34,41	30,60	45,57	14,09	303,22	P × H − проёмы	за вычетом проёмов	л. 12, 13	по КП	
3	Демонтаж существующей отделки потолка до основания	м²	10,57	2,93	20,32	12,91	6,52	3,91	1,51	11,42	6,02	22,48	2,13	100,72	S пом.		л. 12, 13	по КП	
4	Демонтаж существующих дверных блоков	шт	1	1		1	1	1	1	1		1	1	9	по ведомости проёмов		л. 13, 14	по КП	
5	Демонтаж существующих сантехприборов и электрооборудования (если есть)	компл													по факту на объекте		л. 13	по КП	
6	Устройство стяжки: стяжка ЦПС М200, 50 мм	м²	10,62	2,97	20,55	13,22	6,57	3,95	1,55	11,46	6,22	22,57	2,17	101,85	S пом. + S в дверных проёмах (b × t/2)	проёмы добавлены	л. 39–41	530	53 981
7	Гидроизоляция обмазочная, 2 слоя: пол, стены на 200 мм, зоны замачивания	м²						11,45					8,07	19,52	пол + (P − двери) × h заведения + зоны замачивания		л. 35	450	8 784
8	Штукатурка стен по маякам, до 10 мм	м²	32,70	17,61	37,18	35,51	23,54	20,12	11,89	34,41	30,60	45,57	14,09	303,22	P × H − проёмы по обводу коробок − грани перегородок на ГКЛВ	за вычетом проёмов	л. 12, 40, 41	530	160 707
9	Штукатурка оконных откосов шириной более 200 мм	м²	0,99		2,02		0,99			1,01		2,07		7,08	Σ (2h + b) × глубина откоса	откосы > 200 мм	л. 12	540	3 823
Итого по разделу 1 — 227 295 ₽ (позиций 9, из них по КП 5); в сводную смету — л. 95, 96																			
2. Инженерные системы																			
10	Прокладка слаботочной линии: Кабель домофона — тип по системе поставщика, отдельно от силовых	м												4,30	по лучам от ЩС**: 1 точ., запас 10 %		л. 27	по КП	
11	Прокладка слаботочной линии: Кабель коаксиальный RG-6 (75 Ом) к розеткам ТВ, отдельно от силовых	м												50,40	по лучам от ЩС**: 3 точ., запас 10 %		л. 27	по КП	
12	Прокладка слаботочной линии: Кабель U/UTP кат. 6 (LAN, Wi-Fi и камеры по PoE), отдельно от силовых	м												71,50	по лучам от ЩС**: 5 точ., запас 10 %		л. 27	по КП	
13	Прокладка гофротрубы Ø20 для слаботочных линий, отдельно от силовых	м												113,60	по длине лучей без участков в канале плинтуса (≈ 90 %)		л. 27	по КП	
14	Сборка слаботочного щита ЩС**: корпус, патч-панель, подключение линий и питания 220 В; коммутатор и точки доступа — оборудование заказчика	шт												1	один щит		л. 23, 24, 27	по КП	
15	Электроточка: подрозетник в бетоне, розетка, выключатель, вывод	шт	11		10	8	16	4		11	4	10	3	77	по ведомости электроточек		л. 20, 23, 24	950	73 150
16	Штробы в стенах под спуски кабеля к точкам — выполняются только после технического заключения о несущих стенах	м	21,25		19,70	12,05	23,90	5,57		21,25	7,60	19,50	3,91	134,73	Σ (H − h) по точкам на стенах: вертикальные спуски	после техзаключения	л. 13, 20	по КП	
17	Установка встраиваемого точечного светильника	шт	6		8	4	7	3		6	2	8	2	46	по плану освещения		л. 21	750	34 500
18	Монтаж светильника: потолочного, подвесного, настенного	шт	2	1	1			1	1	2		2	1	11	по плану освещения		л. 21	1 200	13 200
19	Монтаж LED-ленты в алюминиевый профиль	м	12,30		5,00	1,80	1,20			12,30		15,50		48,10	Σ длин лент по плану освещения		л. 21	230	11 063
20	Установка блока питания LED в доступном месте (люк, шкаф)	шт	1		1	1	1			1		1		6	один на LED-группу		л. 21	570	3 420
21	Установка автономного пожарного извещателя	шт	1		1	1	1			1	1	1		7	по плану розеток		л. 20	по КП	
22	Сборка щита: установка автоматов и АВДТ групп, вводного автомата	шт												6	группы + вводной автомат		л. 25	230	1 380
23	Установка вводного УЗО	шт												1	по однолинейной схеме		л. 25	380	380

Допущения и предложения на листе

Основа листа: размеры сняты со скана обмерного плана KV design (см): часть подписей не читается, помещения выровнены по читаемым размерам; контрольный обмер не выполнен (К-1); высота потолка 2650 мм принята по отметкам обмера (H = 2,50…2,66 м, ригель 2,28 м) — уточнить при обмере (К-2); толщины стен 300 / 120 мм приняты, межквартирная стена и колонны — по скану, не замерены (К-1); разрешённая мощность 15 кВт принята по типовым ТУ; при объединении двух квартир — переоформление ТУ (К-4).

Знак «**» — предложение проектировщика, заказчиком не утверждено (согласовать с заказчиком): записи в реестре нет: ЩС — щит слаботочный: место и состав.

См. лист открытых вопросов (лист 6, записи К-1, К-2, К-4).

Изм.	Кол.уч	Лист	№ док.	Подп.	Дата
Разраб.		Кырлан А.С.			18.10.26
Пров.					
ГИП					
Н. контр.					
Утв.					

ГД-2026-009-АИ

Квартира 103 м²

Общая площадь 100,72* м² · * размеры со скана, не замерены (реестр — л. 6, К-1)

Дизайн-проект интерьера

Стадия	Лист	Листов
РП	90	96

Ведомость объёмов работ

М б/м

Кырлан Александр Сергеевич

выпуск 18.10.2026 № 53dc234b8d · стр. 102 из 135

Ведомость объёмов работ (продолжение)

Объёмы по помещениям от чертежа · площади в м², длины в м · формула, правило проёмов и источник в каждой строке

Ведомость объёмов работ по помещениям (продолжение)

Поз.	Наименование работ (материал, число слоёв)	Ед. изм.	Объём по помещениям (№ по экспликации)											Всего	Формула подсчёта	Правило проёмов	Источник	Цена за ед., ₽	Стоимость, ₽
			1	2	3	4	5	6	7	8	9	10	11						
24	Монтаж инсталляции, установка подвесного унитаза и кнопки смыва	шт						1					1	2	по плану выводов		л. 30, 32	10 500	21 000
25	Короб инсталляции: каркас и обшивка ГКЛВ в 2 слоя, ревизионный доступ к смыву	шт						1					1	2	по плану выводов		л. 30, 35–38	по КП	
26	Короб К1 над чистым полом: каркас и обшивка ГКЛВ под плитку (материалы — в спецификации ВК)	м.п.						3,55					1,35	4,90	Σ открытых участков выпусков К1 (профиль листа разводки ВК)		л. 30, 32	по КП	
27	Установка ванны с сифоном	шт						1						1	по плану выводов		л. 30, 32	6 000	6 000
28	Установка умывальника (мойки) с сифоном и смесителем	шт						1					1	2	по плану выводов		л. 30, 32	3 000	6 000
29	Установка душевого поддона с трапом, ограждения	шт											1	1	по плану выводов		л. 30, 32	по КП	
30	Подключение стиральной (посудомоечной) машины к ВК	шт							1					1	по плану выводов		л. 30	по КП	
31	Установка радиатора с узлом подключения и терморегулятором	шт	1		2		1			1		2		7	по плану отопления		л. 29	по КП	
Итого по разделу 2 — 170 093 ₽ (позиций 22, из них по КП 12); в сводную смету — л. 95, 96																			
3. Чистовые работы																			
32	Облицовка стен керамогранитом 600×1200 на клею	м²						17,04					11,85	28,89	по раскладке: зона облицовки − место за коробом	за вычетом проёмов	л. 35–38	2 500	72 225
33	Облицовка короба инсталляции (ГКЛВ) керамогранитом: лицо, боковины, полка	м²						1,76					1,47	3,23	по раскладке: лицо, боковины, полка		л. 35–38	2 500	8 075
34	Укладка керамогранита на пол, 600×1200, на клею	м²				13,22		3,95					2,17	19,34	S пом. + S в дверных проёмах	проёмы добавлены	л. 35–39	1 800	34 812
35	Затирка швов керамогранита	м²				12,91		22,71					15,45	51,07	Σ S облицовки и пола из плитки		л. 35–38	150	7 661
36	Грунтование стен, 2 слоя (под штукатурку и под отделку)	м²	32,70	17,61	37,18	35,51	23,54	20,12	11,89	34,41	30,60	45,57	14,09	303,22	P × H − проёмы	за вычетом проёмов	л. 40, 41	96	29 109
37	Шпаклёвка стен под окраску, 2 слоя (старт и финиш), уровень Q3	м²	32,70	17,61	37,18	35,51	23,54		11,89	34,41	30,60	45,57		269,01	P × H − проёмы − фартук	за вычетом проёмов	л. 40, 41	750	201 758
38	Грунтование и шпаклёвка оконных откосов, 2 слоя	м.п.	4,32		8,80		4,30			4,40		8,99		30,81	Σ (2h + b) по окнам	по окнам	л. 12	300	9 243
39	Грунтование потолка, 2 слоя	м²	10,57	2,93	20,32	12,91	6,52	3,91	1,51	11,42	6,02	22,48	2,13	100,72	S пом.		л. 40, 41	96	9 669
40	Шпаклёвка потолка под окраску, 2 слоя, уровень Q3	м²	10,57	2,93	20,32	12,91	6,52	3,91	1,51	11,42	6,02	22,48	2,13	100,72	S пом.		л. 34, 40, 41	950	95 684
41	Окраска потолка водно-дисперсионной краской, 2 слоя	м²	10,57	2,93	20,32	12,91	6,52	3,91	1,51	11,42	6,02	22,48	2,13	100,72	S пом.		л. 40, 41	360	36 259
42	Окраска стен водно-дисперсионной краской, 2 слоя	м²	36,25	19,08	49,40	43,20	27,08		13,36	37,90	37,74	53,05		317,06	P × H − фартук, проёмы не вычитаются	без вычета проёмов	л. 40, 41	300	95 118
43	Окраска оконных откосов, 2 слоя	м.п.	4,32		8,80		4,30			4,40		8,99		30,81	Σ (2h + b) по окнам	по окнам	л. 12	120	3 697
44	Укладка инженерной доски на клей	м²	10,62	2,97	20,55		6,57		1,55	11,46	6,22	22,57		82,51	S пом. + S в дверных проёмах	проёмы добавлены	л. 39–41	1 200	99 012
45	Установка плинтуса МДФ h=80 мм	м.п.	12,88	6,50	14,74	12,64	9,42		4,34	13,60	10,84	18,52		103,48	P − ширина дверных проёмов		л. 40, 41	450	46 566
46	Окраска плинтуса в тоне No. 291, 2 слоя	м.п.	12,88	6,50	14,74	12,64	9,42		4,34	13,60	10,84	18,52		103,48	как плинтус		л. 40, 41	300	31 044
47	Монтаж дверей скрытого монтажа под покраску (поставщик дверей)	шт	1	1			1	1	1	1		1	1	8	по ведомости проёмов		л. 14	5 250	42 000
48	Входная дверь, поставка с монтажом и откосами	шт												1	по ведомости проёмов		л. 14	по КП	
Итого по разделу 3 — 821 932 ₽ (позиций 17, из них по КП 1); в сводную смету — л. 95, 96																			

Допущения и предложения на листе

Основа листа: размеры сняты со скана обмерного плана KV design (см): часть подписей не читается, помещения выровнены по читаемым размерам; контрольный обмер не выполнен (К-1); высота потолка 2650 мм принята по отметкам обмера (H = 2,50…2,66 м, ригель 2,28 м) — уточнить при обмере (К-2); толщины стен 300 / 120 мм приняты, межквартирная стена и колонны — по скану, не замерены (К-1); разрешённая мощность 15 кВт принята по типовым ТУ; при объединении двух квартир — переоформление ТУ (К-4).

См. лист открытых вопросов (лист 6, записи К-1, К-2, К-4).

Изм.	Кол.уч	Лист	№ док.	Подп.	Дата
Разраб.		Кырлан А.С.			18.10.26
Пров.					
ГИП					
Н. контр.					
Утв.					

ГД-2026-009-АИ

Квартира 103 м²

Общая площадь 100,72* м² · * размеры со скана, не замерены (реестр — л. 6, К-1)

Дизайн-проект интерьера

Стадия	Лист	Листов
РП	91	96

Ведомость объёмов работ (продолжение)

М б/м

Кырлан Александр Сергеевич

Ведомость объёмов работ (окончание)

ПРЕДВАРИТЕЛЬНО · не для производства работ · открыто пунктов: 4 (реестр — л. 6)

Объёмы по помещениям от чертежа · площади в м², длины в м · формула, правило проёмов и источник в каждой строке

Ведомость подсчёта площадей по помещениям

№	Помещение	S пола, м²	P, м	H, м	P × H, м²	Проёмы, м²	Стены нетто, м²	В дверных проёмах, м²	Плинтус, м	Откосы, м.п.
1	Кабинет-библиотека	10,57	13,68	2,65	36,25	3,55	32,70	0,05	12,88	4,32
2	Кладовая	2,93	7,20	2,65	19,08	1,47	17,61	0,04	6,50	нет
3	Гостиная-столовая	20,32	18,64	2,65	49,40	12,22	37,18	0,23	14,74	8,80
4	Прихожая-холл	12,91	16,30	2,65	43,20	7,69	35,51	0,31	12,64	нет
5	Кухня	6,52	10,22	2,65	27,08	3,54	23,54	0,05	9,42	4,30
6	Ванная	3,91	8,10	2,67	21,59	1,47	20,12	0,04	нет	нет
7	Постирочная	1,51	5,04	2,65	13,36	1,47	11,89	0,04	4,34	нет
8	Спальня 2	11,42	14,30	2,65	37,90	3,49	34,41	0,04	13,60	4,40
9	Коридор	6,02	14,24	2,65	37,74	7,14	30,60	0,20	10,84	нет
10	Спальня мастер	22,48	20,02	2,65	53,05	7,48	45,57	0,09	18,52	8,99
11	Ванная мастер	2,13	5,84	2,67	15,56	1,47	14,09	0,04	нет	нет
	Итого	**100,72**			**354,20**	**50,99**	**303,21**	**1,14**	**103,48**	**30,82**

Реестр контрольных сумм

Показатель	По ВОР	По чертежу	Расхождение	Лист
Σ площадей помещений без летних, м² — общая площадь по экспликации	100,72	100,72	0,0 %	л. 12
Стены под окраску, м² (шпаклёвка) ведомость отделки	269,01	269,00	0,0 %	л. 40, 41
Потолки под окраску, м² — ведомость отделки	100,72	100,72	0,0 %	л. 40, 41
Плинтус, м — ведомость отделки	103,48	103,48	0,0 %	л. 40, 41
Плитка к заказу, шт — ведомость плитки	124	124	0,0 %	л. 35
Гидроизоляция, м² — ведомость материалов плитки	19,52	19,52	0,0 %	л. 35
Точки ЭОМ, шт — планы ЭОМ (без щитов)	154	156	-1,3 %	л. 20, 21

Примечания

1. Объёмы — от геометрии проекта (та же, что на планах и в ведомости отделки), не от общей площади: P — периметр чистого контура, H — от чистого пола до низа потолка, проёмы — по наружному обводу коробок.
2. Подсчёт по ГЭСН-2001-15 и ГЭСН-2001-11: штукатурка и шпаклёвка стен — за вычетом проёмов; окраска водными составами — без вычета проёмов (п. 2.24); откосы — отдельно, по ширине до 200 и более 200 мм; полы — с площадью в дверных проёмах.
3. Плитка — по раскладке (целые и с подрезкой); короб инсталляции и фартук — отдельными строками, двойного счёта облицовки нет. Материалы, запас и количество к заказу — в спецификации материалов.
4. Цены — ориентир по открытым прайсам Москвы (цены на 21.09.2026), не коммерческое предложение; «по КП» — расценки нет, строка в итог не входит.
5. Демонтаж — по плану демонтажа и общим указаниям: покрытия пола, отделка стен и потолков, дверные блоки — до основания; объёмы справочные, уточняются по факту на объекте (расценки в книге нет — «по КП»).
6. Штробы в стенах — только после технического заключения о несущих стенах (общие указания, план обмера и демонтажа): строка «Штробы в стенах» вертикальные спуски кабеля от потолочной трассы к точкам, объём не меньше фактического (горизонтальные трассы — по исполнительной схеме). Расценки штробления в прайсе нет — «по КП», в итог не входит; кабель в штробах стен прокладывается после неё.
7. Площадь облицовки стен — одно число с тремя названиями: зона облицовки по ведомости отделки 30,57 м² − место за коробом инсталляции 1,68 м² (плитку туда не кладут) = стены под плитку 28,89 м² (строка «Облицовка стен»); облицовка коробов 3,23 м² — отдельной строкой; стены и короба вместе — 32,12 м² (столько плитки по раскладке в спецификации). Источник — один (quantities.js), расхождение на листах ловит.
8. Слаботочные сети: кабель по лучам от ЩС** 126,20 м (U/UTP, RG-6, домофон — по видам), гофра 113,60 м, щит ЩС** с патч-панелью; розетки RJ45 и ТВ монтируются в строке «Электроточка». Длины те же, что в ведомости изделий электрика (одна модель — lowcurrent-engineer/bom.js); оборудование заказчика (точки доступа, камеры, коммутатор) в спецификацию не входит. 1 точ. — предложение листа слаботочки.
9. Коробы: стояков (нет) и К1 над чистым полом (4,90 м открытых участков; труба К1 вдоль стен 11,14 м в короб не зашивается — она за приборами, в раме инсталляции и в шахтах). В спецификации ВК короб К1 заказывается с запасом 10 % — 5,40 м. Материалы коробов стояков и инсталляции — в спецификации материалов, К1 — в спецификации ВК.

Допущения и предложения на листе

Основа листа: размеры сняты со скана обмерного плана KV design (см): часть подписей не читается, помещения выровнены по читаемым размерам; контрольный обмер не выполнен (К-1); высота потолка 2650 мм принята по отметкам обмера (H = 2,50…2,66 м, ригель 2,28 м) — уточнить при обмере (К-2); толщины стен 300 / 120 мм приняты, межквартирная стена и колонны — по скану, не замерены (К-1); разрешённая мощность 15 кВт принята по типовым ТУ; при объединении двух квартир — переоформление ТУ (К-4).
Знак «**» — предложение проектировщика, заказчиком не утверждено (согласовать с заказчиком): записи в реестре нет: ЩС — щит слаботочный: место и состав.
См. лист открытых вопросов (лист 6, записи К-1, К-2, К-4).

Изм.	Кол.уч	Лист	№ док.	Подп.	Дата
Разраб.		Кырлан А.С.			18.10.26
Пров.					
ГИП					
Н. контр.					
Утв.					

ГД-2026-009-АИ

Квартира 103 м²

Общая площадь 100,72* м² · * размеры со скана, не замерены (реестр — л. 6, К-1)

Дизайн-проект интерьера

Стадия	Лист	Листов
РП	92	96

Ведомость объёмов работ (окончание)

М б/м

Кырлан Александр Сергеевич

Спецификация материалов

ПРЕДВАРИТЕЛЬНО · не для производства работ · открыто пунктов: 4 (реестр — л. 6)

Отделочные материалы: чистое количество, запас, упаковка, к заказу · ГОСТ 21.110-2013

Спецификация материалов (ГОСТ 21.110-2013, форма 1)

Поз.	Наименование и техническая характеристика	Тип, марка, артикул	Код продукции	Поставщик	Ед. изм.	Количество				Масса ед., кг	Примечание
						чистое	запас, %	упаковка	к заказу		
Покрытия полов и облицовка											
1	Инженерная доска (дуб натуральный, рабочий слой 4 мм, эмиссия E1, прямая укладка)	1167-4250			м²	82,52	7	по артикулу	88,30 м²		пом. 1, 2, 3, 5, 7, 8, 9, 10; до целой упаковки; л. 39–41
2	Клей для паркетной и инженерной доски (эластичный, по ТУ изготовителя доски)	по выбору подрядчика			м²	82,52		ведро по ТУ	по ТУ		расход кг/м² — по ТУ клея; л. 39
3	Керамогранит 600×600 мм под травертин	аналог: керамогранит под травертин			шт	23	10	коробка	26 шт		3 целых + 20 с подрезкой; 6,04 м² по раскладке, к заказу 9,36 м²; пом. 6, 11; л. 35–38
4	Керамогранит 600×1200 мм под травертин	аналог: керамогранит под травертин			шт	66	10	коробка	76 шт		19 целых + 47 с подрезкой; 32,12 м² по раскладке, к заказу 54,72 м²; пом. 6, 11; л. 35–38
5	Керамогранит 600×1200 мм A8UZ	A8UZ			шт	20	10	коробка	22 шт		0 целых + 20 с подрезкой; 12,91 м² по раскладке, к заказу 15,84 м²; пом. 4; л. 35–38
Сухие смеси и гидроизоляция											
6	Клей плиточный цементный класса C2 TE S1 (ГОСТ Р 56387-2018)	Ceresit CM 17 или аналог			кг	367,78	10	мешок 25 кг	17 меш.	25	слой 5 мм, 1,50 кг/м² на 1 мм; л. 35
7	Затирка цементная класса CG2WA, цвет — по колерной карте	Mapei Ultracolor Plus 132 или аналог			кг	3,65	10	упак. 2 кг	3 упак.	2	расход (a+b)/ab × шов × t × 1,6 кг/м²; л. 35
8	Гидроизоляция обмазочная полимерная, 2 слоя, лента в углах, манжеты на выводах	по выбору подрядчика			м²	19,52	10	ведро по ТУ	по ТУ		пом. 6, 11; расход кг/м² — по ТУ; л. 35
9	Лента демпферная по периметру пола из плитки	по выбору подрядчика			м	24,68	10	рулон	28,00 м		л. 35
10	Смесь цементно-песчаная для стяжки М200 (50 мм, 55 мм, 53 мм, 33 мм)	по выбору подрядчика			м³	5,11	5	мешок по ТУ	по ТУ		S 101,85 м² × толщина; армирование и маяки — по ТУ; л. 39
11	Смесь штукатурная гипсовая для машинного и ручного нанесения по маякам, слой до 10 мм	по выбору подрядчика			м²	303,22	10	мешок по ТУ	по ТУ		пом. 1, 2, 3, 4, 5, 6, 7, 8, 9, 10, 11; расход кг/м² на 1 мм слоя — по ТУ смеси, толщина — по замеру кривизны стен; л. 12, 40, 41
Короба из ГКЛВ											
12	Лист ГКЛВ 12,5 мм, 2500 × 1200 мм, обшивка коробов в 2 слоя	по выбору подрядчика			м²	6,46	10	лист 3,00 м²	3,00 лист		инсталляция пом. 6: 1,76 м²; инсталляция пом. 11: 1,47 м²; площадь × 2 слоя; короб К1 над полом — в спецификации ВК; л. 30, 35–38
13	Профиль стальной оцинкованный 27 × 28 мм: каркас коробов (стойки и направляющие)	по выбору подрядчика			м	15,60	10	хлыст 3 м	6 шт		стойки через 400 мм по свободному периметру + направляющие по полу и потолку; крепёж, лента, шпаклёвка швов — по узлу короба; л. 30, 35–38
Слаботочные сети											
14	Кабель домофона — тип по системе поставщика	по выбору подрядчика			м	4,30		бухта по ТУ	5,00 м		по лучам от ЩС**, 1 точ., запас 10 % уже в длине; 1 точ. — предложение листа слаботочки (знак «*» на плане); л. 27
15	Кабель коаксиальный RG-6 (75 Ом) к розеткам ТВ	по выбору подрядчика			м	50,40		бухта по ТУ	51,00 м		по лучам от ЩС**, 3 точ., запас 10 % уже в длине; 1 точ. — предложение листа слаботочки (знак «*» на плане); л. 27
16	Кабель U/UTP кат. 6 (LAN, Wi-Fi и камеры по PoE)	по выбору подрядчика			м	71,50		бухта по ТУ	72,00 м		по лучам от ЩС**, 5 точ., запас 10 % уже в длине; 1 точ. — предложение листа слаботочки (знак «*» на плане); л. 27
17	Гофротруба Ø20 для слаботочных линий, отдельно от силовых	по выбору подрядчика			м	113,60		бухта по ТУ	114,00 м		по длине лучей без участков в канале плинтуса (≈ 90 %); л. 27
18	Розетка компьютерная RJ45, кат. 6, с рамкой и подрозетником	по выбору подрядчика			шт	4		шт	4 шт		LAN1, LAN2; серия механизмов — как у розеток и выключателей; л. 23, 24, 27
19	Розетка телевизионная (коаксиальная) с рамкой и подрозетником	по выбору подрядчика			шт	3		шт	3 шт		ТВ1, ТВ2; серия механизмов — как у розеток и выключателей; л. 23, 24, 27

Допущения и предложения на листе

Основа листа: размеры сняты со скана обмерного плана KV design (см): часть подписей не читается, помещения выровнены по читаемым размерам; контрольный обмер не выполнен (К-1); высота потолка 2650 мм принята по отметкам обмера (Н = 2,50…2,66 м, ригель 2,28 м) — уточнить при обмере (К-2); толщины стен 300 / 120 мм приняты, межквартирная стена и колонны — по скану, не замерены (К-1); разрешённая мощность 15 кВт принята по типовым ТУ; при объединении двух квартир — переоформление ТУ (К-4).

Знак «**» — предложение проектировщика, заказчиком не утверждено (согласовать с заказчиком): записи в реестре нет: ЩС — щит слаботочный: место и состав; плинтус пом. 1–5, 7–10, акцент пом. 3, фартук пом. 5 — артикул изделия не выбран: позиция описана характеристиками («аналог по характеристикам»), артикул выбирается при закупке.

См. лист открытых вопросов (лист 6, записи К-1, К-2, К-4).

Изм.	Кол.уч	Лист	№ док.	Подп.	Дата
Разраб.		Кырлан А.С.			18.10.26
Пров.					
ГИП					
Н. контр.					
Утв.					

ГД-2026-009-АИ

Квартира 103 м²

Общая площадь 100,72* м² · * размеры со скана, не замерены (реестр — л. 6, К-1)

Дизайн-проект интерьера

Стадия	Лист	Листов
РП	93	96

Спецификация материалов

М б/м

Кырлан Александр Сергеевич

Спецификация материалов (окончание)

Отделочные материалы: чистое количество, запас, упаковка, к заказу · ГОСТ 21.110-2013

Спецификация материалов (ГОСТ 21.110-2013, форма 1) (продолжение)

Поз.	Наименование и техническая характеристика	Тип, марка, артикул	Код продукции	Поставщик	Ед. изм.	Количество				Масса ед., кг	Примечание
						чистое	запас, %	упаковка	к заказу		
20	Трубка или монитор домофона (поставка домофонной организации)	по выбору подрядчика			шт	1		шт	1 шт		ДФ1; серия механизмов — как у розеток и выключателей; л. 23, 24, 27
21	Щит слаботочный ЩС**: корпус, DIN-рейка, розетки 220 В	по выбору подрядчика			шт	1		шт	1 шт		ЩС**; серия механизмов — как у розеток и выключателей; л. 23, 24, 27
22	Патч-панель, портов не менее 5	по выбору подрядчика			шт	1		шт	1 шт		серия механизмов — как у розеток и выключателей; л. 23, 24, 27
Лакокрасочные материалы											
23	Краска интерьерная акриловая, матовая, класс истирания 1	Farrow & Ball Modern Emulsion No. 289 «Inchyra Blue — тёмный сине-серый»			л	8,88	10	банка 2,5 л	4 банк		36,99 м² × 2 сл. × 0,12 л/м²; пом. 1, 8, 10; л. 40, 41
24	Краска интерьерная акриловая, матовая, класс истирания 1	Farrow & Ball Modern Emulsion No. 291 «School House White — тёплый меловой белый»			л	34,03	10	банка 2,5 л	15 банк		141,79 м² × 2 сл. × 0,12 л/м²; пом. 1, 4, 8, 9, 10; л. 40, 41
25	Краска интерьерная акриловая, глубокоматовая, класс истирания 2	Tikkurila Anti-Reflex 2 S 0502-Y «Белый с лёгкой желтизной»			л	16,28	10	банка 2,7 л	7 банк		67,84 м² × 2 сл. × 0,12 л/м²; пом. 1 (пот.), 2 (пот.), 4 (пот.), 7 (пот.), 8 (пот.), 9 (пот.), 10 (пот.); л. 40, 41
26	Краска интерьерная акриловая, матовая, класс истирания 1	Tikkurila Harmony S 0502-Y «Белый с лёгкой желтизной»			л	7,08	10	банка 2,7 л	3 банк		29,50 м² × 2 сл. × 0,12 л/м²; пом. 2, 7; л. 40, 41
27	Краска интерьерная акриловая, матовая, класс истирания 2	Tikkurila Optiva 5 Matt No. 255 «Tanner's Brown — тёмный шоколад»			л	4,44	10	банка 2,7 л	2 банк		12,33 м² × 3 сл. × 0,12 л/м²; пом. 3; л. 40, 41
28	Краска интерьерная акриловая, матовая, класс истирания 2	Tikkurila Optiva 5 Matt No. 291 «School House White — тёплый меловой белый»			л	5,96	10	банка 2,7 л	3 банк		24,85 м² × 2 сл. × 0,12 л/м²; пом. 3; л. 40, 41
29	Краска интерьерная акриловая, глубокоматовая, класс истирания 2	Tikkurila Anti-Reflex 2 No. 291 «School House White — тёплый меловой белый»			л	4,88	10	банка 2,7 л	2 банк		20,32 м² × 2 сл. × 0,12 л/м²; пом. 3 (пот.); л. 40, 41
30	Краска интерьерная акриловая, полуматовая, класс истирания 1	Tikkurila Luja 7 No. 291 «School House White — тёплый меловой белый»			л	5,65	10	банка 2,7 л	3 банк		23,54 м² × 2 сл. × 0,12 л/м²; пом. 5; л. 40, 41
31	Краска интерьерная акриловая, матовая, класс истирания 1	Tikkurila Luja 7 No. 291 «School House White — тёплый меловой белый»			л	1,56	10	банка 2,7 л	1 банк		6,52 м² × 2 сл. × 0,12 л/м²; пом. 5 (пот.); л. 40, 41
32	Краска интерьерная акриловая, матовая, класс истирания 1	Tikkurila Luja 7 S 0502-Y «Белый с лёгкой желтизной»			л	1,45	10	банка 2,7 л	1 банк		6,04 м² × 2 сл. × 0,12 л/м²; пом. 6 (пот.), 11 (пот.); л. 40, 41
33	Шпаклёвка финишная полимерная под окраску (стены и потолки, Q3)	по выбору подрядчика			м²	369,73	10	ведро по ТУ	по ТУ		расход кг/м² на слой — по ТУ; л. 40, 41
34	Грунтовка акриловая глубокого проникновения, 2 слоя	по выбору подрядчика			м²	403,94	10	канистра по ТУ	по ТУ		расход л/м² — по ТУ; л. 40, 41
Погонажные изделия и потолки											
35	Плинтус напольный МДФ под покраску, h=80 мм, крепление к стене	аналог: плинтус МДФ под покраску 80×16			м.п.	79,32	10	хлыст 2,4 м	37 шт		пом. 1, 2, 4, 7, 8, 9, 10; длина хлыста — по артикулу; л. 40, 41
36	Плинтус напольный МДФ под покраску, h=80 мм, крепление к стене	аналог: плинтус МДФ под окраску 80×16 мм			м.п.	24,16	10	хлыст 2,4 м	12 шт		пом. 3, 5; длина хлыста — по артикулу; л. 40, 41

Примечания

1. Чистое количество — из ведомости объёмов работ и раскладки плитки; запас — отдельной графой (доска — по ведомости отделки, плитка, краска и плинтус — 10 %); «к заказу» — с запасом и кратно упаковке.
2. Плитка — штуками по раскладке, запас на каждую поверхность. Калибр (рабочий размер) и тон — одной партией на помещение, калибр указать при заказе и сверить с раскладкой до укладки.
3. Краска — 0,12 л/м² на слой (середина вилки 0,10–0,15 л/м²) по фактической площади окраски из ведомости отделки; колеровка одной партией.
4. «По ТУ» — расход задаёт производитель выбранного продукта; количество к заказу — после выбора марки.
5. Поз. 3, 4, 35, 36 заданы характеристиками («аналог:»): марку, артикул и поставщика согласовать с заказчиком до закупки, без артикула не заказывать.
6. Штукатурная смесь — на ту же площадь, что строка ВОР «Штукатурка стен» (303,22 м²): площадь одна, расход смеси задаёт производитель.
7. Коробы инсталляции и стояков: ГКЛВ в 2 слоя и профиль 27 × 28 мм считаются по свободным граням коробов (источник — раскладка плиточника и шахты в данных); короб К1 над полом — в спецификации ВК.
8. Потолки ГКЛ: в этой спецификации — площадь системы П113; число листов, профилей и подвесов — по шагам каркаса на листе потолков (подвесы через 1000, несущие через 500, основные через 1200 мм), схема каркаса не выпущена. Сантехника, светильники и мебель — по своим спецификациям.

Допущения и предложения на листе

Основа листа: размеры сняты со скана обмерного плана KV design (см): часть подписей не читается, помещения выровнены по читаемым размерам; контрольный обмер не выполнен (К-1); высота потолка 2650 мм принята по отметкам обмера (Н = 2,50…2,66 м, ригель 2,28 м) — уточнить при обмере (К-2); толщины стен 300 / 120 мм приняты, межквартирная стена и колонны — по скану, не замерены (К-1); разрешённая мощность 15 кВт принята по типовым ТУ; при объединении двух квартир — переоформление ТУ (К-4).

Знак «**» — предложение проектировщика, заказчиком не утверждено (согласовать с заказчиком): записи в реестре нет: ЩС — щит слаботочный: место и состав; плинтус пом. 1–5, 7–10, акцент пом. 3, фартук пом. 5 — артикул изделия не выбран: позиция описана характеристиками («аналог по характеристикам»), артикул выбирается при закупке.

См. лист открытых вопросов (лист 6, записи К-1, К-2, К-4).

Изм.	Кол.уч	Лист	№ док.	Подп.	Дата

Разраб.	Кырлан А.С.		18.10.26
Пров.			
ГИП			
Н. контр.			
Утв.			

ГД-2026-009-АИ

Квартира 103 м²

Общая площадь 100,72* м² · * размеры со скана, не замерены (реестр — л. 6, К-1)

Дизайн-проект интерьера	Стадия	Лист	Листов
	РП	94	96

Спецификация материалов (окончание)

М б/м

Кырлан Александр Сергеевич

Смета ориентировочная

ПРЕДВАРИТЕЛЬНО · не для производства работ · открыто пунктов: 4 (реестр — л. 6)

Работы, материалы, оборудование, услуги и резерв · цены — ориентир по открытым прайсам, не коммерческое предложение

Сводная смета (цены на 21.09.2026, Москва)

№	Наименование работ, материалов, услуг	Ед. изм.	Кол-во	Цена за ед., ₽	Стоимость, ₽			Чей подряд	Срок поставки, дн.	Основание	Источник цены
					план	факт	разница				
Работы — по ведомости объёмов работ											
1	Демонтаж и черновые работы (без 5 поз. по КП)	раздел	1		227 295			бригада		ВОР, поз. 1–9; л. 90–92	по ВОР
2	Инженерные системы (без 12 поз. по КП)	раздел	1		170 093			бригада		ВОР, поз. 10–31; л. 90–92	по ВОР
3	Чистовые работы (без 1 поз. по КП)	раздел	1		821 932			бригада, поставщик		ВОР, поз. 32–48; л. 90–92	по ВОР
Материалы — по спецификации материалов											
4	Инженерная доска	м²	88,30	4 513	398 498			поставщик		спецификация, поз. 1	Ц7
5	Керамогранит 600×600 мм	м²	9,36	1 800	16 848			поставщик		спецификация, поз. 3	Ц6
6	Керамогранит 600×1200 мм	м²	70,56	3 500	246 960			поставщик		спецификация, поз. 4, 5	Ц6
7	Клей плиточный цементный класса C2 TE S1	меш.	17	1 800	30 600			поставщик		спецификация, поз. 6	Ц7
8	Затирка цементная класса CG2WA	упак.	3	1 000	3 000			поставщик		спецификация, поз. 7	Ц7
9	Краска Farrow & Ball Modern Emulsion, банка 2,5 л	банк	19	5 800	110 200			поставщик		спецификация, поз. 23, 24	Ц7
10	Краска Tikkurila (Anti-Reflex 2, Harmony, Optiva 5 Matt, Luja 7), банка 2,7 л	банк	22	3 510	77 220			поставщик		спецификация, поз. 25, 26, 27, 28, 29, 30, 31, 32	Ц6
11	Плинтус напольный МДФ под покраску	шт	49	368	18 032			поставщик		спецификация, поз. 35, 36	Ц7
12	Прочие материалы с расходом по ТУ (клей для доски, гидроизоляция, демпферная лента, смесь для стяжки, смесь штукатурная гипсовая для машинного и ручного нанесения по маякам, лист гклв 12, профиль стальной оцинкованный 27 × 28 мм: каркас коробов (стойки и направляющие), кабель слаботочки, гофра слаботочки, изделия слаботочки, шпаклёвка, грунтовка)	компл	1	по КП				поставщик		спецификация, поз. 2, 8, 9, 10, 11, 12, 13, 14, 15, 16, 17, 18, 19, 20, 21, 22, 33, 34	
Оборудование и мебель — поставка по спецификациям											
13	Кухонный гарнитур по проекту кухни, изготовление и монтаж (4–8 нед.)	компл	1	по КП				поставщик	уточн.; ориентир 4–8 нед. от замера	л. 57–60	

Допущения и предложения на листе

Основа листа: размеры сняты со скана обмерного плана KV design (см): часть подписей не читается, помещения выровнены по читаемым размерам; контрольный обмер не выполнен (К-1); высота потолка 2650 мм принята по отметкам обмера (Н = 2,50…2,66 м, ригель 2,28 м) — уточнить при обмере (К-2); толщины стен 300 / 120 мм приняты, межквартирная стена и колонны — по скану, не замерены (К-1); разрешённая мощность 15 кВт принята по типовым ТУ; при объединении двух квартир — переоформление ТУ (К-4).

См. лист открытых вопросов (лист 6, записи К-1, К-2, К-4).

Изм.	Кол.уч	Лист	№ док.	Подп.	Дата
Разраб.		Кырлан А.С.			18.10.26
Пров.					
ГИП					
Н. контр.					
Утв.					

ГД-2026-009-АИ

Квартира 103 м²

Общая площадь 100,72* м² · * размеры со скана, не замерены (реестр — л. 6, К-1)

Дизайн-проект интерьера

Стадия	Лист	Листов
РП	95	96

Смета ориентировочная

М б/м

Кырлан Александр Сергеевич

Смета ориентировочная (окончание)

ПРЕДВАРИТЕЛЬНО · не для производства работ · открыто пунктов: 4 (реестр — л. 6)

Работы, материалы, оборудование, услуги и резерв · цены — ориентир по открытым прайсам, не коммерческое предложение

Сводная смета (цены на 21.09.2026, Москва) (продолжение)

№	Наименование работ, материалов, услуг	Ед. изм.	Кол-во	Цена за ед., ₽	Стоимость, ₽			Чей подряд	Срок поставки, дн.	Основание	Источник цены
					план	факт	разница				
14	Двери скрытого монтажа с коробом под покраску, поставка	шт	8	по КП				поставщик	уточн.; ориентир ≈ 30 дн.	л. 14	
15	Оборудование заказчика слаботочных сетей: точка доступа wi-fi — 1 шт; коммутатор — 1 шт	компл	1	по КП				заказчик		л. 23, 24	
16	Сантехника, светильники, мебель и предметы интерьера	компл	1	по КП				поставщик		л. 32; л. 33; л. 62; л. 17–19	
Прочие работы и услуги											
17	Вынос и вывоз строительного мусора	м³		по факту				бригада		после демонтажа	
18	Подъём материалов на этаж (лифтом или вручную — по договору)	т		по факту				бригада		по массе поставки	
19	Доставка чистовых материалов, 10 % от поставки			10 %	90 136			поставщик		от суммы материалов	
20	Уборка после ремонта	м²	100,72	по факту				бригада		S квартиры	
	Итого работы				**1 219 320**						
	Итого материалы				**901 358**						
	Итого прочие услуги				**90 136**						
	Резерв на непредвиденные работы и материалы, 15 %				**331 622**						
	ВСЕГО ориентировочно (без оборудования и позиций по КП)				**2 542 436**						

Примечания

1. Смета ориентировочная, не коммерческое предложение: объёмы — из ведомости объёмов работ и спецификации материалов, цены — нижняя граница открытых прайсов Москвы (цены на 21.09.2026); перед договором цены подтвердить у подрядчика и поставщиков.
2. Источники цен: Ц1 — Домашний мастерок: прайс на отделочные работы, 2026; Ц2 — Домашний мастерок: прайс на плиточные работы, 2026; Ц3 Домашний мастерок: прайс на электромонтажные работы, 2026; Ц4 — Профи ремонтник: штукатурно-малярные работы; Ц5 — Profi.ru: укладка керамогранита на стены, Москва 2026; Ц6 — knowledge/spec-materials.md, разд. 1 и 3: ориентир по сегментам; Ц7 — Розница Москвы, 09.2026: Лемана ПРО, KGSnab, официальный дилер Farrow & Ball.
3. В итог не вошли позиции «по КП» и «по факту»: оборудование и мебель, двери, материалы с расходом по ТУ, вывоз мусора, подъём и уборка.
4. Доставка — 10 % от материалов, резерв — 15 % (частный ремонт 10–20 %) отдельными строками, в количествах не спрятаны. Графы «факт» и «разница» заполняются по актам.

Допущения и предложения на листе

Основа листа: размеры сняты со скана обмерного плана KV design (см): часть подписей не читается, помещения выровнены по читаемым размерам; контрольный обмер не выполнен (К-1); высота потолка 2650 мм принята по отметкам обмера (Н = 2,50…2,66 м, ригель 2,28 м) — уточнить при обмере (К-2); толщины стен 300 / 120 мм приняты, межквартирная стена и колонны — по скану, не замерены (К-1); разрешённая мощность 15 кВт принята по типовым ТУ; при объединении двух квартир — переоформление ТУ (К-4).
См. лист открытых вопросов (лист 6, записи К-1, К-2, К-4).

Изм.	Кол.уч	Лист	№ док.	Подп.	Дата
Разраб.		Кырлан А.С.			18.10.26
Пров.					
ГИП					
Н. контр.					
Утв.					

ГД-2026-009-АИ

Квартира 103 м²

Общая площадь 100,72* м² · * размеры со скана, не замерены (реестр — л. 6, К-1)

Дизайн-проект интерьера

Стадия	Лист	Листов
РП	96	96

Смета ориентировочная (окончание)

М б/м

Кырлан Александр Сергеевич

11

Визуализации

Кырлан Александр Сергеевич

выпуск 18.10.2026 · 53dc234b8d · стр. 109 из 135

Планировочное решение · вид сверху

Квартира 103 м² · визуализация 1 из 26

выпуск 18.10.2026 № 53dc234b8d · стр. 110 из 135

room-bath1-wB

Квартира 103 м² · визуализация 2 из 26

room-bath1-wC

Квартира 103 м² · визуализация 3 из 26

выпуск 18.10.2026 № 53dc234b8d · стр. 112 из 135

выпуск 18.10.2026 № 53dc234b8d · стр. 113 из 135

room-bath1-wD

room-bath2-wide

Квартира 103 м² · визуализация 5 из 26

выпуск 18.10.2026 № 53dc234b8d · стр. 114 из 135

room-bedroom1-wA

Квартира 103 м² · визуализация 6 из 26

выпуск 18.10.2026 № 53dc234b8d · стр. 115 из 135

room-bedroom1-wB

Квартира 103 м² · визуализация 7 из 26

выпуск 18.10.2026 № 53dc234b8d · стр. 116 из 135

room-bedroom1-wD

Квартира 103 м² · визуализация 8 из 26

room-bedroom2-wA

Квартира 103 м² · визуализация 9 из 26

выпуск 18.10.2026 № 53dc23408d · стр. 118 из 135

room-bedroom2-wB

Квартира 103 м² · визуализация 10 из 26

выпуск 18.10.2026 № 53dc2348d8d · стр. 119 из 135

room-bedroom2-wC

Квартира 103 м² · визуализация 11 из 26

выпуск 18.10.2026 № 53dc234b8d · стр. 120 из 135

room-bedroom2-wD

выпуск 18.10.2026 № 53dc234b8d · стр. 121 из 135

room-corridor-wB

Квартира 103 м² · визуализация 13 из 26

room-hall-wA

room-hall-wB

Квартира 103 м² · визуализация 15 из 26

выпуск 18.10.2026 № 53dc2348d8d · стр. 125 из 135

room-kitchen-wB

выпуск 18.10.2026 № 53dc234b8d · стр. 126 из 135

room-kitchen-wC

выпуск 18.10.2026 № 53dc234b8d · стр. 127 из 135

room-living-wA

room-living-wB

выпуск 18.10.2026 № 53dc234b8d · стр. 129 из 135

room-living-wC

room-living-wD

Квартира 103 м² · визуализация 21 из 26

выпуск 18.10.2026 № 53dc234b8d · стр. 130 из 135

room-storage-wide

выпуск 18.10.2026 № 53dc234b8d · стр. 131 из 135

room-study-wA

Квартира 103 м² · визуализация 23 из 26

выпуск 18.10.2026 № 53dc234b8d · стр. 132 из 135

room-study-wB

Квартира 103 м² · визуализация 24 из 26

выпуск 18.10.2026 № 53dc234b8d · стр. 133 из 135

room-study-wD

Квартира 103 м² · визуализация 25 из 26

room-wardrobe-wide

выпуск 18.10.2026 № 53dc234b8d · стр. 135 из 135