ДИЗАЙН-ПРОЕКТ ИНТЕРЬЕРА

Квартира 103 м²

ретро с авторской мебелью

100,72 м²

оптимизм · функциональность · тёплое дерево · лёгкость · ретро без китча · связь с улицей · графичные акценты

Ретро 2026: mid-century 65 % + ар-деко (art-deco.json) 35 %. Стены — School House White No. 291 и кремовый S 1005-Y20R, потолки — белый S 0502-Y; второй план — орех и тик, оливковый Bancha No. 298, сине-серый Inchyra Blue No. 289; акценты — горчица S 2050-Y20R, терракота S 3050-Y70R, тил S 5030-B10G, изумрудный бархат S 5040-B90G; металл — латунь. Мебель — авторские модели середины века (как предложение, модели уточняются с заказчиком).

ПАЛИТРА 60 / 30 / 10

F&B No. 291	NCS S 1005-Y20R	NCS S 0502-Y	F&B No. 298	F&B No. 289
60 %	60 %	60 %	30 %	30 %



Визуализация 1 · Вид сверху (3D): планировка с мебелью, текстилем и декором

ОБЪЕКТ	ОБЩАЯ ПЛОЩАДЬ	ПОМЕЩЕНИЙ
Квартира 103 м²	100,72 м²	11, из них жилых 4

СТИЛЬ	СТАДИЯ	ШИФР
Мид-сенчури · ретро с авторской мебелью	Рабочий проект	ГД-2026-009-АИ

АВТОР ПРОЕКТА

Кырлан Александр Сергеевич

Октябрь 2026

					Проект: Квартира 103 м²
	Лист	№ док.	Подпись	Дата	Титульный лист
Дизайнер	Кырлан А.С.			18.10.26	

Стадия	Лист	Листов
П	1	103

выпуск 18.10.2026 № d119044df4 · стр. 1 из 103

Список листов

Лист	Наименование
1	Титульный лист
2	Список листов
3	План планировки от заказчика
4	План монтажный
5	Кухня (пом. 5). Монтажная схема
6	Кухня (пом. 5). Монтажная схема
7	Шкафы. Монтажная схема
8	Карта покрытий стен
9	Колерная карта
10	План размещения мебели и оборудования
11	Спецификация мебели и оборудования
12	Спецификация мебели и оборудования (продолжение)
13	Спецификация мебели и оборудования (продолжение)
14	Ведомости изделий, техники и фурнитуры
15	План выводов сантехники
16	Схема разводки водопровода и канализации
17	Спецификация сантехнического оборудования
18	Раскладка плитки. Ванная. Развёртки стен
19	Раскладка плитки. Ванная мастер. Развёртки стен
20	План размещения дверей
21	План потолков
22	План розеток и электровыводов
23	План слаботочных сетей
24	План освещения
25	Спецификация светильников и сценарии освещения
26	Управление светильниками
27	План вентиляции
28	План отопления
29	План покрытий пола
30	Раскладка плитки. Планы полов
31	Раскладка плитки. Прихожая-холл
32	Визуализация. Вид сверху
33	Визуализация: Кабинет-библиотека
34	Визуализация: Кабинет-библиотека
35	Визуализация: Кабинет-библиотека
36	Развёртка стены А. Кабинет-библиотека (пом. 1)
37	Развёртка стены Б. Кабинет-библиотека (пом. 1)
38	Развёртка стены В. Кабинет-библиотека (пом. 1)
39	Развёртка стены Г. Кабинет-библиотека (пом. 1)
40	Визуализация кладовой

Лист	Наименование
41	Развёртки стен. Кладовая (пом. 2)
42	Визуализация: Гостиная-столовая
43	Визуализация: Гостиная-столовая
44	Визуализация: Гостиная-столовая
45	Визуализация: Гостиная-столовая
46	Развёртка стены А. Гостиная-столовая (пом. 3)
47	Развёртка стены Б. Гостиная-столовая (пом. 3)
48	Развёртка стены В. Гостиная-столовая (пом. 3)
49	Развёртка стены Г. Гостиная-столовая (пом. 3)
50	Визуализация: Прихожая-холл
51	Визуализация: Прихожая-холл
52	Развёртка стены А. Прихожая-холл (пом. 4)
53	Развёртка стены Б. Прихожая-холл (пом. 4)
54	Развёртка стены В. Прихожая-холл (пом. 4)
55	Развёртка стены Г. Прихожая-холл (пом. 4)
56	Визуализация кухни
57	Визуализация кухни
58	Развёртка стены А. Кухня (пом. 5), кухонный фронт
59	Развёртка стены Б. Кухня (пом. 5), кухонный фронт
60	Развёртка стены В. Кухня (пом. 5), кухонный фронт
61	Развёртка стены Г. Кухня (пом. 5)
62	Визуализация ванной
63	Визуализация ванной
64	Визуализация ванной
65	Развёртки стен А, Б. Ванная (пом. 6)
66	Развёртки стен В, Г. Ванная (пом. 6)
67	Визуализация постирочной
68	Развёртки стен А, Б, В. Постирочная (пом. 7)
69	Развёртка стены Г. Постирочная (пом. 7)
70	Визуализация: Спальня 2
71	Визуализация: Спальня 2
72	Визуализация: Спальня 2
73	Развёртка стены А. Спальня 2 (пом. 8)
74	Развёртка стены Б. Спальня 2 (пом. 8)
75	Развёртка стены В. Спальня 2 (пом. 8)
76	Развёртка стены Г. Спальня 2 (пом. 8)
77	Визуализация коридора
78	Развёртка стены А. Коридор (пом. 9)
79	Развёртка стены Б. Коридор (пом. 9)
80	Развёртка стены В. Коридор (пом. 9)

Лист	Наименование
81	Развёртка стены Г. Коридор (пом. 9)
82	Визуализация: Спальня мастер
83	Визуализация: Спальня мастер
84	Визуализация: Спальня мастер
85	Визуализация: Спальня мастер
86	Развёртка стены А. Спальня мастер (пом. 10)
87	Развёртка стены Б. Спальня мастер (пом. 10)
88	Развёртка стены В. Спальня мастер (пом. 10)
89	Развёртка стены Г1. Спальня мастер (пом. 10)
90	Развёртка стены Г2. Спальня мастер (пом. 10)
91	Визуализация: Ванная мастер
92	Развёртки стен А, Б. Ванная мастер (пом. 11)
93	Развёртки стен В, Г. Ванная мастер (пом. 11)
Д_1	Система хранения М_05
Д_2	Шкаф-купе М_11
Д_3	Система хранения М_21
Д_4	Шкаф распашной М_23
Д_5	Шкаф распашной М_28
Д_6	Кухня (пом. 5). Развёртка гарнитура
Д_7	Кухня (пом. 5). Развёртка гарнитура
С1	Ведомость отделки помещений. Лист 1 из 2
С2	Спецификация отделочных материалов
С3	Узлы

	Лист	№ док.	Подпись	Дата
Дизайнер	Кырлан А.О.			18.10.26


Проект: Квартира 103 м²

Список листов	Стадия	Лист	Листов
	П	2	103

выпуск 18.10.2026 № d119044df4 · стр. 2 из 103


Отметки по высоте

±0,000	чистый пол пом. 1–5, 7–10; отсчёт высот
−0,015	чистый пол пом. 6, 11, ниже на 15 мм
плита	верх плиты разный: −0,064, −0,170 (задание на обмер)
сущ. пол	снимается до плиты; не замерен (задание на обмер)

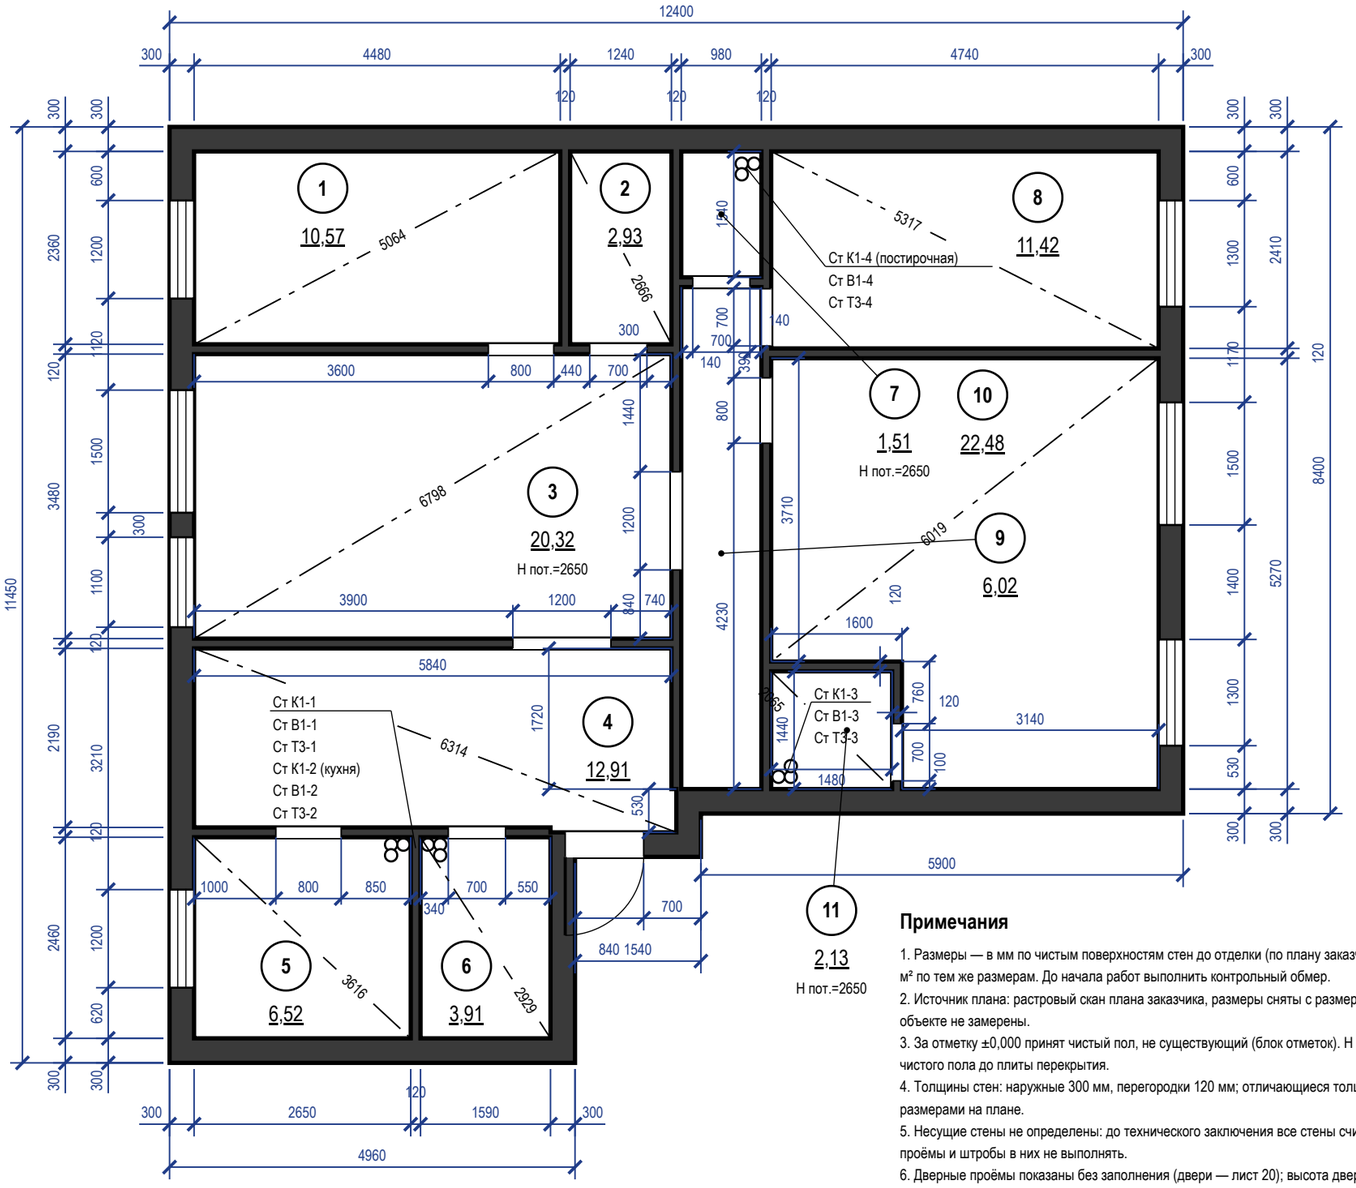
12400
300
4480
1240
980
4740
300
120
120
120
1
10,57
2
2,93
8
11,42
5064
2666
5317
Ст К1-4 (постирочная)
Ст В1-4
Ст Т3-4
7
1,51
10
22,48
Н пот.=2650
3
20,32
Н пот.=2650
6798
6019
9
6,02
3900
1200
840
740
1600
5840
Ст К1-1
Ст В1-1
Ст Т3-1
Ст К1-2 (кухня)
Ст В1-2
Ст Т3-2
6314
4
12,91
Ст К1-3
Ст В1-3
Ст Т3-3
3140
1480
5900
1000
800
850
700
550
340
700
840 1540
5
6,52
3616
6
3,91
2929
11
2,13
Н пот.=2650
2650
1590
4960
11450
2360
3480
2190
2460
3210
1200
1500
1100
620
1440
1200
3710
4230
1720
1440
760
700
530
1300
2410
1170
1500
1400
5270
8400
1300
530
3600
800
440
700
3600
140
700
700
140
800
300
120
120
120
120
120
120
120
120
120
300
300
300

Экспликация помещений

№	Наименование	Площадь, м²
1	Кабинет-библиотека	10,57
2	Кладовая	2,93
3	Гостиная-столовая	20,32
4	Прихожая-холл	12,91
5	Кухня	6,52
6	Ванная	3,91
7	Постирочная	1,51
8	Спальня 2	11,42
9	Коридор	6,02
10	Спальня мастер	22,48
11	Ванная мастер	2,13
	Итого (общая площадь)	**100,72**

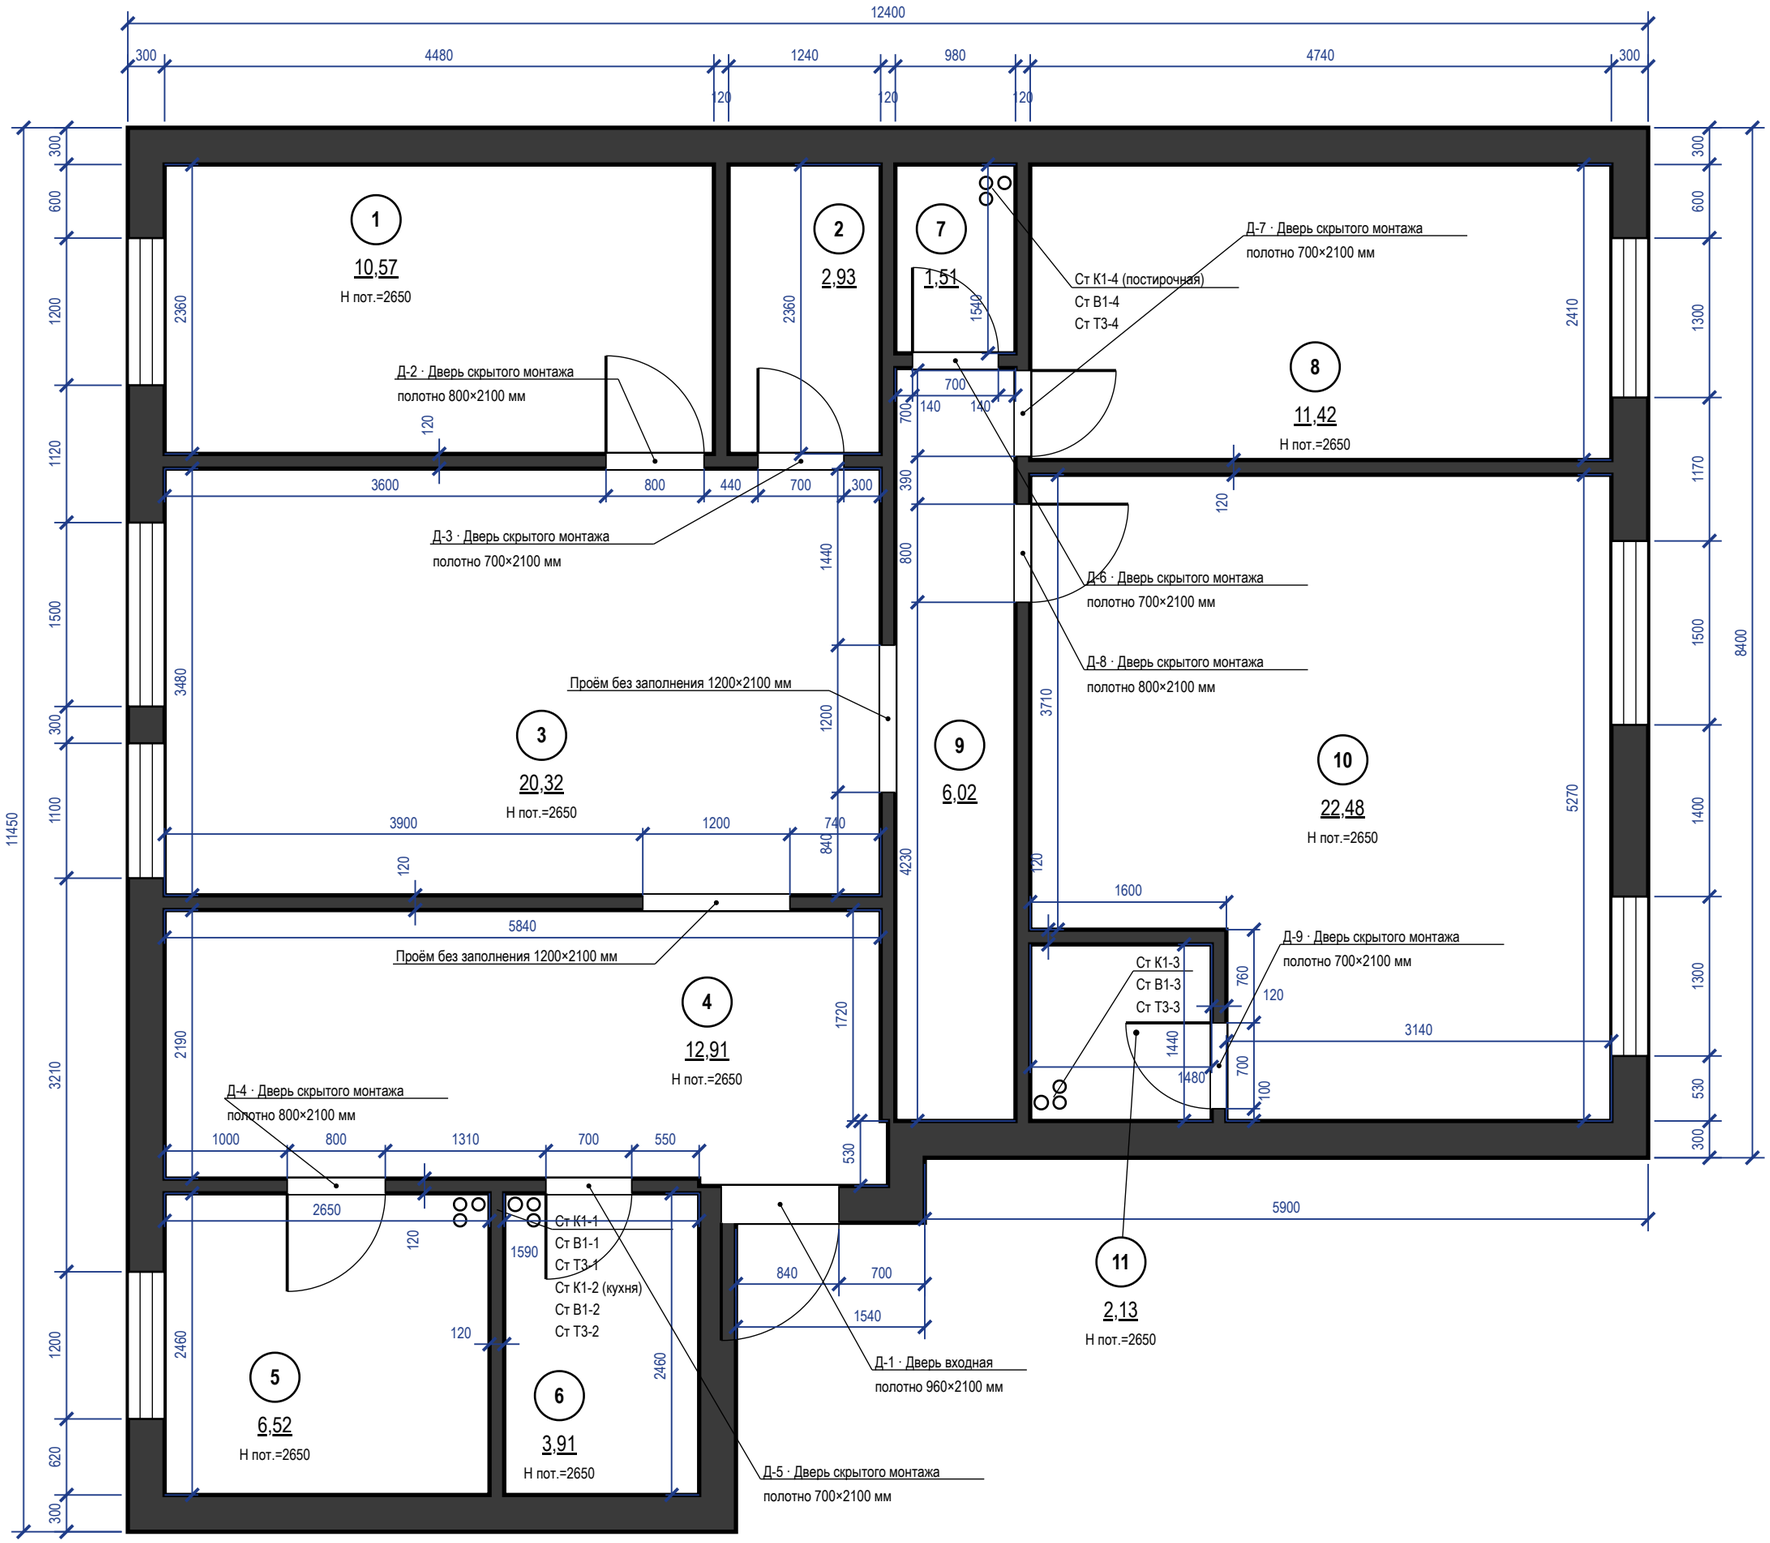

Примечания


1. Размеры — в мм от чистовых поверхностей стен до отделки; размеры уточнить по месту до начала работ.
2. Новые перегородки и облицовки — синим; каркас и обшивка — по выноскам; двери и проёмы — лист 20.
3. Несущие стены не изменять: проёмы, ниши и штробы в них — только по техническому заключению.
4. Размеры короче 1 мм на листе цепочкой не показаны (две выносные линии на таком расстоянии сливаются): пом. 9, стена Б — 20 мм от угла до проёма.

					Проект: Квартира 103 м²
	Лист	№ док.	Подпись	Дата	План монтажный
Дизайнер	Кырлан А.С.			18.10.26	


Стадия	Лист	Листов
П	4	103

выпуск 18.10.2026 № d119044df4 · стр. 4 из 103

Привязка выводов и крепление модулей

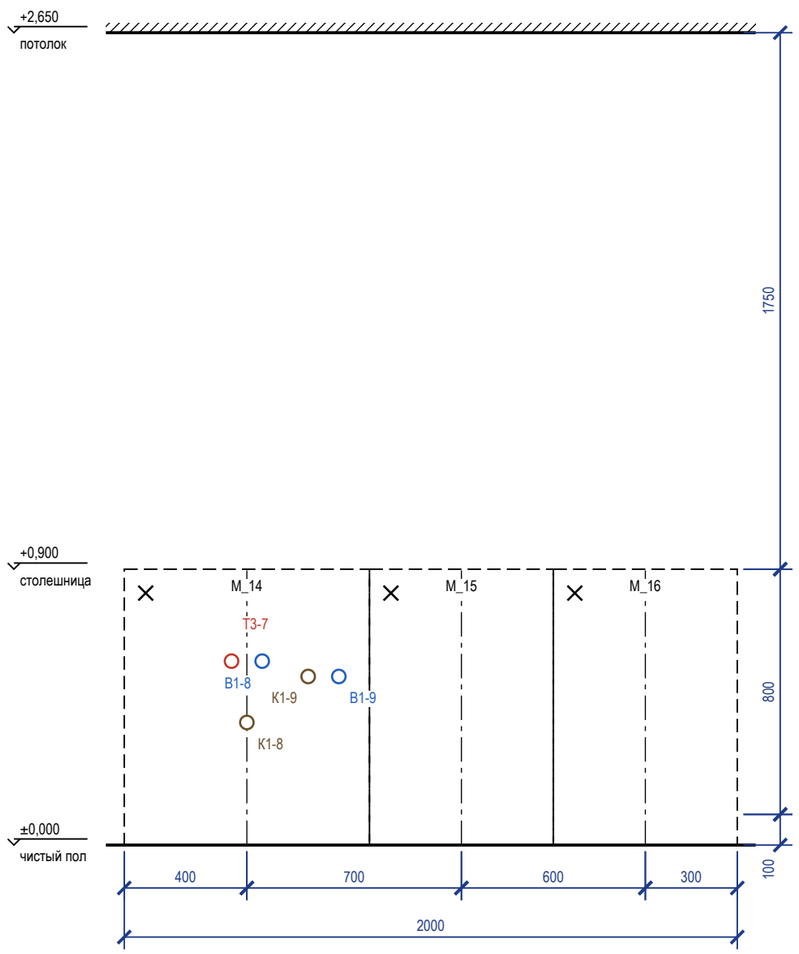

План столешницы

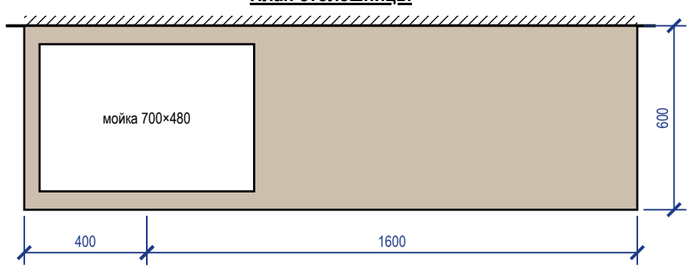

Привязка выводов к осям модулей

Код	Назначение	Модуль	От оси, мм	H, мм	Размещение
T3-7	T3 — межос. 100	M_14	−50	600	в модуле мойки
K1-8	K1 Ø50 — мойка	M_14	0	400	в модуле мойки
B1-8	B1 — межос. 100	M_14	+50	600	в модуле мойки
K1-9	K1 Ø40 — слив ПММ в шкафу мойки	M_14	+200	550	в модуле мойки
B1-9	B1 — кран ПММ в шкафу мойки	M_14	+300	550	в модуле мойки

Зазоры под отделку

Поверхность	Отделка	Зазор, мм	Учесть
фартук	керамогранит	10	от чернового основания до корпуса навесных и столешницы
стены	окраска	5	под штукатурку и шпаклёвку за пеналом
пол	инженерная доска		цоколь — после укладки пола, опоры ±20 мм

Условные обозначения

- навесной модуль (невидимый контур)
- ось модуля (от неё — привязка вывода)
- анкер / уголок крепления к стене
- розетка на стене
- вывод кабеля к технике
- B1 — вывод воды B1 / T3, канализации K1

Примечания

1. Выводы — по проекту электрики и ВК; привязка по горизонтали — от оси модуля (плюс — вправо по виду), по высоте — от чистого пола до оси вывода.
2. Пенал — уголки к стене 2 шт. сверху; нижние модули — стяжками между собой и уголком к стене; ряд выставить по уровню опорами цоколя.
3. Розетки над столешницей — не ниже 150 мм над ней и не за корпусом техники; розетка за ПММ, духовым шкафом и холодильником — только в соседнем модуле или в зоне цоколя с доступом.
4. Столешница — вырезы по шаблонам выбранных моделей мойки и варочной панели; торцы у стены — герметик, пристеночный плинтус.


	Лист	№ док.	Подпись	Дата
Дизайнер	Кырлан А.С.			18.10.26

Проект: Квартира 103 м²


Кухня (пом. 5). Монтажная схема

Стадия	Лист	Листов
П	5	103

Привязка выводов и крепление модулей

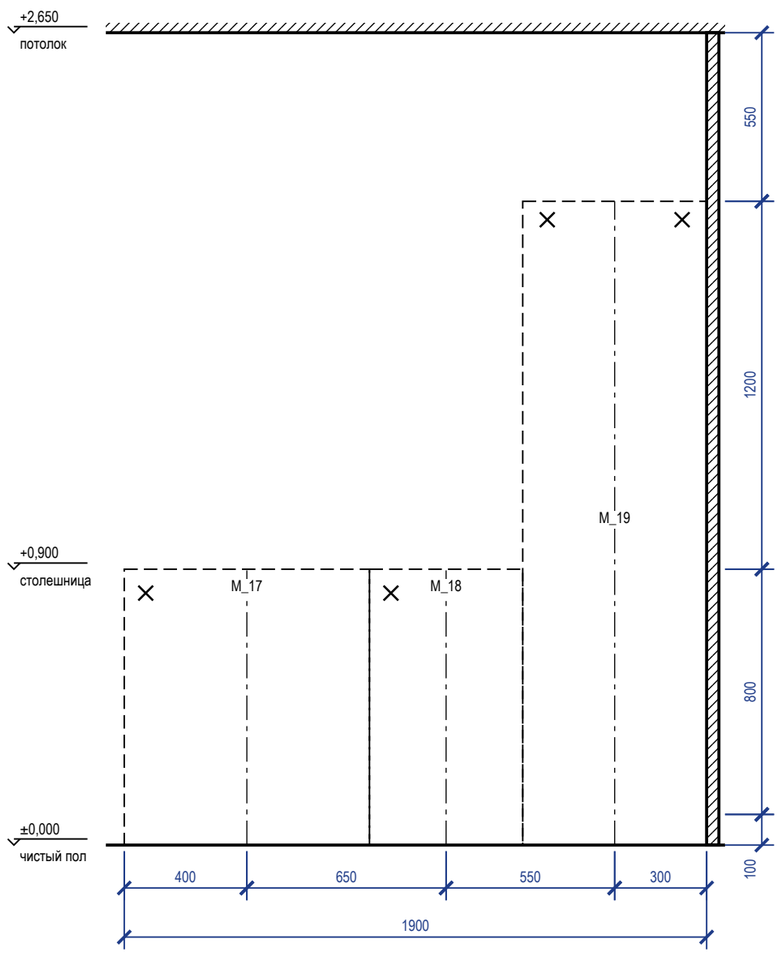

План столешницы

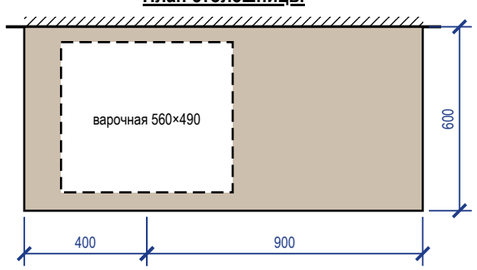

Привязка выводов к осям модулей

Код	Назначение	Модуль	От оси, мм	Н, мм	Размещение

Зазоры под отделку

Поверхность	Отделка	Зазор, мм	Учесть
фартук	керамогранит	10	от чернового основания до корпуса навесных и столешницы
стены	окраска	5	под штукатурку и шпаклёвку за пеналом
пол	инженерная доска		цоколь — после укладки пола, опоры ±20 мм

Условные обозначения

- навесной модуль (невидимый контур)
- ось модуля (от неё — привязка вывода)
- анкер / уголок крепления к стене
- розетка на стене
- вывод кабеля к технике
- B1 — вывод воды B1 / Т3, канализации К1

Примечания


1. Выводы — по проекту электрики и ВК; привязка по горизонтали — от оси модуля (плюс — вправо по виду), по высоте — от чистого пола до оси вывода.
2. Пенал — уголки к стене 2 шт. сверху; нижние модули — стяжками между собой и уголком к стене; ряд выставить по уровню опорами цоколя.
3. Розетки над столешницей — не ниже 150 мм над ней и не за корпусом техники; розетка за ПММ, духовым шкафом и холодильником — только в соседнем модуле или в зоне цоколя с доступом.
4. Столешница — вырезы по шаблонам выбранных моделей мойки и варочной панели; торцы у стены — герметик, пристеночный плинтус.

					Проект: Квартира 103 м²
	Лист	№ док.	Подпись	Дата	Кухня (пом. 5). Монтажная схема
Дизайнер	Кырлан А.С.			18.10.26	


Стадия	Лист	Листов
П	6	103

выпуск 18.10.2026 · d119044df4 · стр. 6 из 103


Система хранения M_05 (пом. 2)

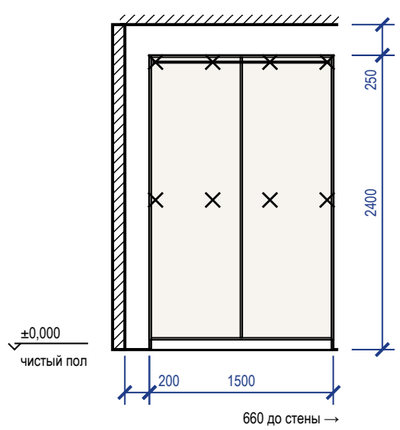


Шкаф-купе M_11 (пом. 4)

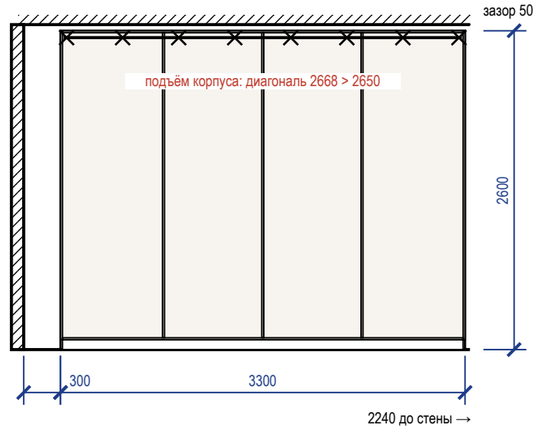


Система хранения M_21 пом. 7

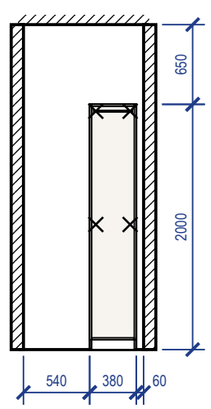

Шкаф распашной M_23 (пом. 8)

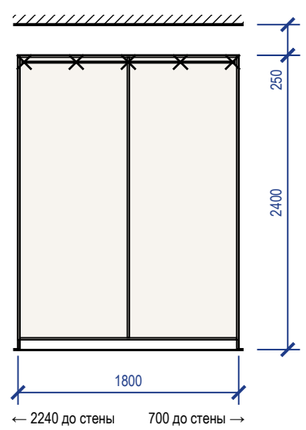

Шкаф распашной M_28 (пом. 10)

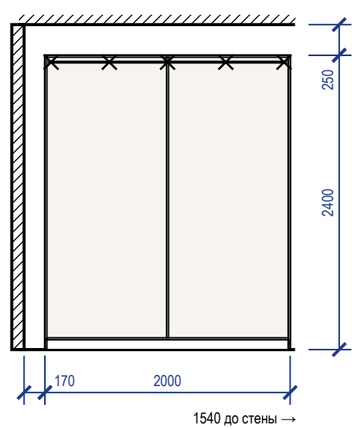

Крепление и зазоры под отделку

Марка	Помещение, стена	Основание	Отделка стены	Зазор, мм	Крепёж по планке	От опрокидывания
M_05	Кладовая (2), стена Б	по основанию — см. таблицу крепежа	окраска	5	анкер 8 шт. (2 ряда)	уголки 2 шт.
M_11	Прихожая-холл (4), стена А	по основанию — см. таблицу крепежа	окраска	5	анкер 8 шт., шаг 457	уголки 2 шт.
M_21	Постирочная (7), стена А	по основанию — см. таблицу крепежа	окраска	5	анкер 4 шт. (2 ряда)	уголки 2 шт.
M_23	Спальня 2 (8), стена А	по основанию — см. таблицу крепежа	окраска	5	анкер 5 шт., шаг 425	уголки 2 шт.
M_28	Спальня мастер (10), стена Г	по основанию — см. таблицу крепежа	окраска	5	анкер 5 шт., шаг 475	уголки 2 шт.

Крепёж по основанию стены

Основание стены	Крепёж
бетон, ж/б	анкер-шуруп 7,5×72 или дюбель 8×60 с шурупом 5×70
кирпич полнотелый	дюбель 8×80 с шурупом 5×90
газобетон, пазогребень	дюбель для газобетона 10×100 или химический анкер
гипсокартон	закладная до обшивки (брус 40×80 или фанера 18 мм), саморез в закладную

Условные обозначения


- × — анкер / уголок крепления к стене
- прямоугольник — корпус и полки ЛДСП (вид на стену)
- штриховка — компенсатор — короб до потолка

Примечания

1. Установочные размеры — от чистого пола и чистых стен; перед установкой контрольный замер после отделки.
2. Порядок: корпус выставить по уровню опорами цоколя → закрепить к стене по задней планке → навесить двери и фасады, отрегулировать зазоры → подогнать и закрепить компенсатор.
3. Анкеры — с шагом не более 500 мм, не ближе 50 мм от края планки; на ГКЛ только в закладную, установленную до обшивки.
4. Скрытые коммуникации под анкеры проверить детектором; трассы электрики по плану розеток.

					Проект: Квартира 103 м²
	Лист	№ док.	Подпись	Дата	
Дизайнер	Кырлан А.С.			18.10.26	Шкафы. Монтажная схема

Стадия	Лист	Листов
П	7	103

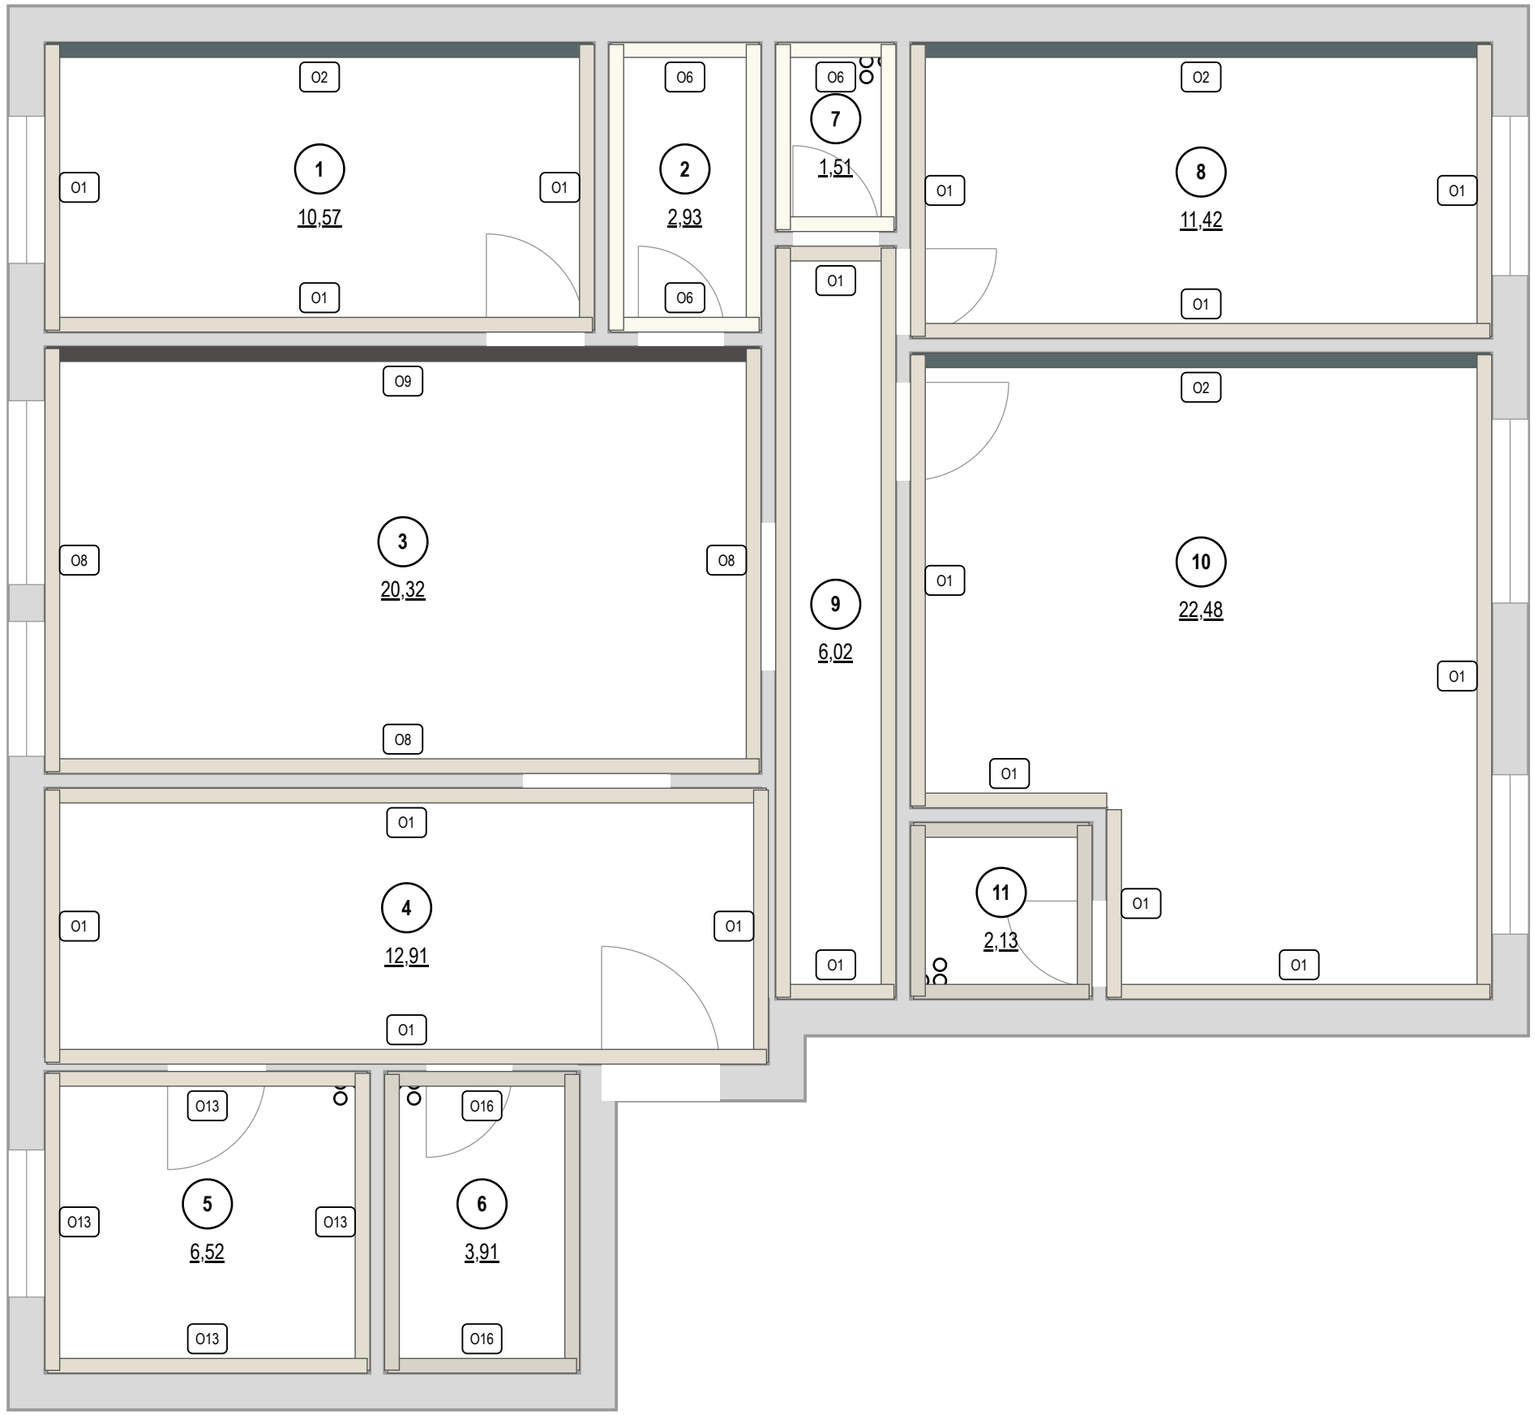

Покрытия стен

Марка	Покрытие	Помещение: S, м²	Итого, м²
O1	окраска Farrow & Ball · No. 291 «School House White — тёплый меловой белый»	1: 20,6; 4: 35,2; 8: 21,6; 9: 30,3; 10: 32,6	140,3
O2	окраска Farrow & Ball · No. 289 «Inchyra Blue — тёмный сине-серый»	1: 11,8; 8: 12,5; 10: 12,5	36,8
O6	окраска Tikkurila · S 0502-Y «Белый с лёгкой желтизной»	2: 17,3; 7: 11,6	28,9

					Проект: Квартира 103 м²
	Лист	№ док.	Подпись	Дата	
Дизайнер	Кырлан А.С.			18.10.26	Карта покрытий стен

Стадия	Лист	Листов
П	8	103

выпуск 18.10.2026 · d119044df4 · стр. 8 из 103

Колерная карта по помещениям

Помещение	Поверхность	Образец	Поз.	Система и код цвета	Производитель, линейка / материал, артикул	Блеск	Класс EN 13300	LRV	Площадь
1. Кабинет-библиотека 10,57 м²	стены		**K1**	Farrow & Ball No. 291	Farrow & Ball · Modern Emulsion	матовая	1	73	20,8 м²
	акцент А		**K2**	Farrow & Ball No. 289	Farrow & Ball · Modern Emulsion	матовая	1	13	11,9 м²
	потолок		**K3**	NCS S 0502-Y	Tikkurila · Anti-Reflex 2	глубокомат.	2	95	10,6 м²
	пол		**KM1**	по образцу	Coswick · Вековые традиции				10,6 м²
	плинтус		**K4**	Farrow & Ball No. 291	МДФ · в цвет Farrow & Ball			73	12,9 м
2. Кладовая 2,93 м²	стены		**K5**	NCS S 0502-Y	Tikkurila · Harmony	матовая	1	95	17,6 м²
	потолок		**K3**	NCS S 0502-Y	Tikkurila · Anti-Reflex 2	глубокомат.	2	95	2,9 м²
	пол		**KM1**	по образцу	Coswick · Вековые традиции				2,9 м²
	плинтус		**K6**	NCS S 0502-Y	МДФ · в цвет NCS			95	6,5 м
3. Гостиная-столовая 20,32 м²	стены		**K7**	Farrow & Ball No. 291	Tikkurila · Optiva 5 Matt	матовая	2	73	24,9 м²
	акцент А		**K8**	Farrow & Ball No. 255	Tikkurila · Optiva 5 Matt	матовая	2	7	12,3 м²
	потолок		**K9**	Farrow & Ball No. 291	Tikkurila · Anti-Reflex 2	глубокомат.	2	73	20,3 м²
	пол		**KM1**	по образцу	Coswick · Вековые традиции				20,3 м²
	плинтус		**K10**	Farrow & Ball No. 291	МДФ · в цвет Farrow & Ball	полуглянц.	2	73	14,7 м
4. Прихожая-холл 12,91 м²	стены		**K1**	Farrow & Ball No. 291	Farrow & Ball · Modern Emulsion	матовая	1	73	35,5 м²
	потолок		**K3**	NCS S 0502-Y	Tikkurila · Anti-Reflex 2	глубокомат.	2	95	12,9 м²
	пол		**K11**	Atlas Concorde A8UZ	Atlas Concorde · Marvel Travertine				12,9 м²
	плинтус		**K4**	Farrow & Ball No. 291	МДФ · в цвет Farrow & Ball			73	12,6 м
5. Кухня 6,52 м²	стены		**K12**	Farrow & Ball No. 291	Tikkurila · Luja 7	полуматов.	1	73	21,9 м²
	потолок		**K13**	Farrow & Ball No. 291	Tikkurila · Luja 7	матовая	1	73	6,5 м²
	пол		**KM1**	по образцу	Coswick · Вековые традиции				6,5 м²
	плинтус		**K10**	Farrow & Ball No. 291	МДФ · в цвет Farrow & Ball	полуглянц.	2	73	9,4 м
	фартук		**KM2**	тон Paper F497 (тёплый белый)	керамогранит · аналог по хар.				1,7 м²

Схема палитры проекта


Стиль: Мид-сенчури 65% + Ар-деко 35% · схема: complement

основной	основной	основной	второстепенный	второстепенный	второстепенный	акцентный	акцентный	акцентный	акцентный
Farrow & Ball No. 291	NCS S 1005-Y20R	NCS S 0502-Y	Farrow & Ball No. 298	Farrow & Ball No. 289	Farrow & Ball No. 255	NCS S 2050-Y20R	NCS S 3050-Y70R	NCS S 5030-B10G	NCS S 5040-B90G
School House White — тёплый меловой белый LRV 73 стены 1,3,4,5,8,9,10; плинтус 1,3,4,5,8,9,10; потолок 5,5; текстиль/декор 3	Светлый кремовый LRV 77 текстиль/декор 1,3,5,8,10	Белый с лёгкой желтизной LRV 95 потолок 1,2,4,6,7,8,9,10,11; стены 2,7; плинтус 2,7; текстиль/декор 1,8,10	Bancha — оливковый середины века LRV 14 текстиль/декор 3,10	Inchyra Blue — тёмный сине-серый LRV 13 акцент 1,8,10; текстиль/декор 1,8,10	Tanner's Brown — тёмный шоколад LRV 7 акцент 3; текстиль/декор 3	Горчичный LRV 42 текстиль/декор 1,8	Терракотовый / жжёный оранжевый LRV 18 текстиль/декор 1,8	Тил LRV 12 текстиль/декор 8	Изумрудный LRV 8 в отделке не применён

План 60/30/10



Окраска, факт — по площади стен, акцентов, потолков

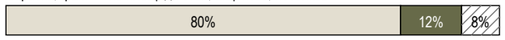

окрашено всего 398,6 м²; второстепенный тон несут мебель и текстиль

Условные обозначения

- **K1** Farrow & Ball No. 291 · School House White — тёплый меловой белый · Modern Emulsion · матовая · кл. 1
- **K2** Farrow & Ball No. 289 · Inchyra Blue — тёмный сине-серый · Modern Emulsion · матовая · кл. 1
- **K3** NCS S 0502-Y · Белый с лёгкой желтизной · Tikkurila Anti-Reflex 2 · глубокомат. · кл. 2
- **K4** Farrow & Ball No. 291 · School House White — тёплый меловой белый · МДФ
- **K5** NCS S 0502-Y · Белый с лёгкой желтизной · Tikkurila Harmony · матовая · кл. 1
- **K6** NCS S 0502-Y · Белый с лёгкой желтизной · МДФ
- **K7** Farrow & Ball No. 291 · School House White — тёплый меловой белый · Optiva 5 Matt · матовая · кл. 2
- **K8** Farrow & Ball No. 255 · Tanner's Brown — тёмный шоколад · Optiva 5 Matt · матовая · кл. 2
- дерево (доска, паркет, ламинат) — рисунок досок
- керамогранит, плитка, камень — сетка швов по формату
- HEX не задан — цвет только по коду и вееру
- **K9** Farrow & Ball No. 291 · School House White — тёплый меловой белый · Anti-Reflex 2 · глубокомат. · кл. 2
- **K10** Farrow & Ball No. 291 · School House White — тёплый меловой белый · МДФ · полуглянц. · кл. 2
- **K11** Atlas Concorde A8UZ · Marvel Travertine · Marvel Travertine
- **K12** Farrow & Ball No. 291 · School House White — тёплый меловой белый · Luja 7 · полуматов. · кл. 1
- **K13** Farrow & Ball No. 291 · School House White — тёплый меловой белый · Luja 7 · матовая · кл. 1
- **K14** NCS S 0502-Y · Белый с лёгкой желтизной · Tikkurila Luja 7 · матовая · кл. 1
- **KM1** инженерная доска · 1167-4250
- **KM2** аналог: керамогранит матовый, тон F497, 600×600×9 мм


K — позиция окраски (код + продукт + блеск), KM — позиция материала, тон KM — по описанию артикула, эталон — образец материала; ≈ LRV — расчёт по HEX, справочно

Примечания

1. Цвет утверждается только по выкрасу на объекте: формат от А3 до 1000×1000 мм на загрунтованном ГКЛ, в 2 слоя (как на стене), не на белой шпаклёвке; смотреть днём и при свете проекта своего помещения, рядом с образцами пола и фасадов. Подпись на обороте: код, бренд и веер, дата.
2. Колеровка машинная в колеровочном центре бренда; каждый код — за один проход, одной партией на весь объём. Колеровщику передаётся только система и код утверждённого веера; плашки и HEX на листе — ориентир, печать не является эталоном цвета.
3. Класс мокрого истирания — EN 13300 (ISO 11998); блеск — по ГОСТ 31975 (ISO 2813), геометрия 60°. LRV — пересчёт координаты L каталога производителя ($Y = ((L^*+16)/116)^3$); «≈» — расчёт по HEX, справочно.
4. Площади поверхностей — тем же способом и с теми же цифрами, что в ведомости отделки (способ счёта — в общих указаниях); объём краски к заказу, фасовка и материалы KM — в спецификации отделочных материалов.
5. Колерная карта на 2 листах: обозначения повторены на каждом, схема квартиры и палитра — на первом, перечень выкрасов — на последнем.

					Проект: Квартира 103 м²
	Лист	№ док.	Подпись	Дата	Колерная карта
Дизайнер	Кырлан А.С.			18.10.26	

Стадия	Лист	Листов
П	9	103

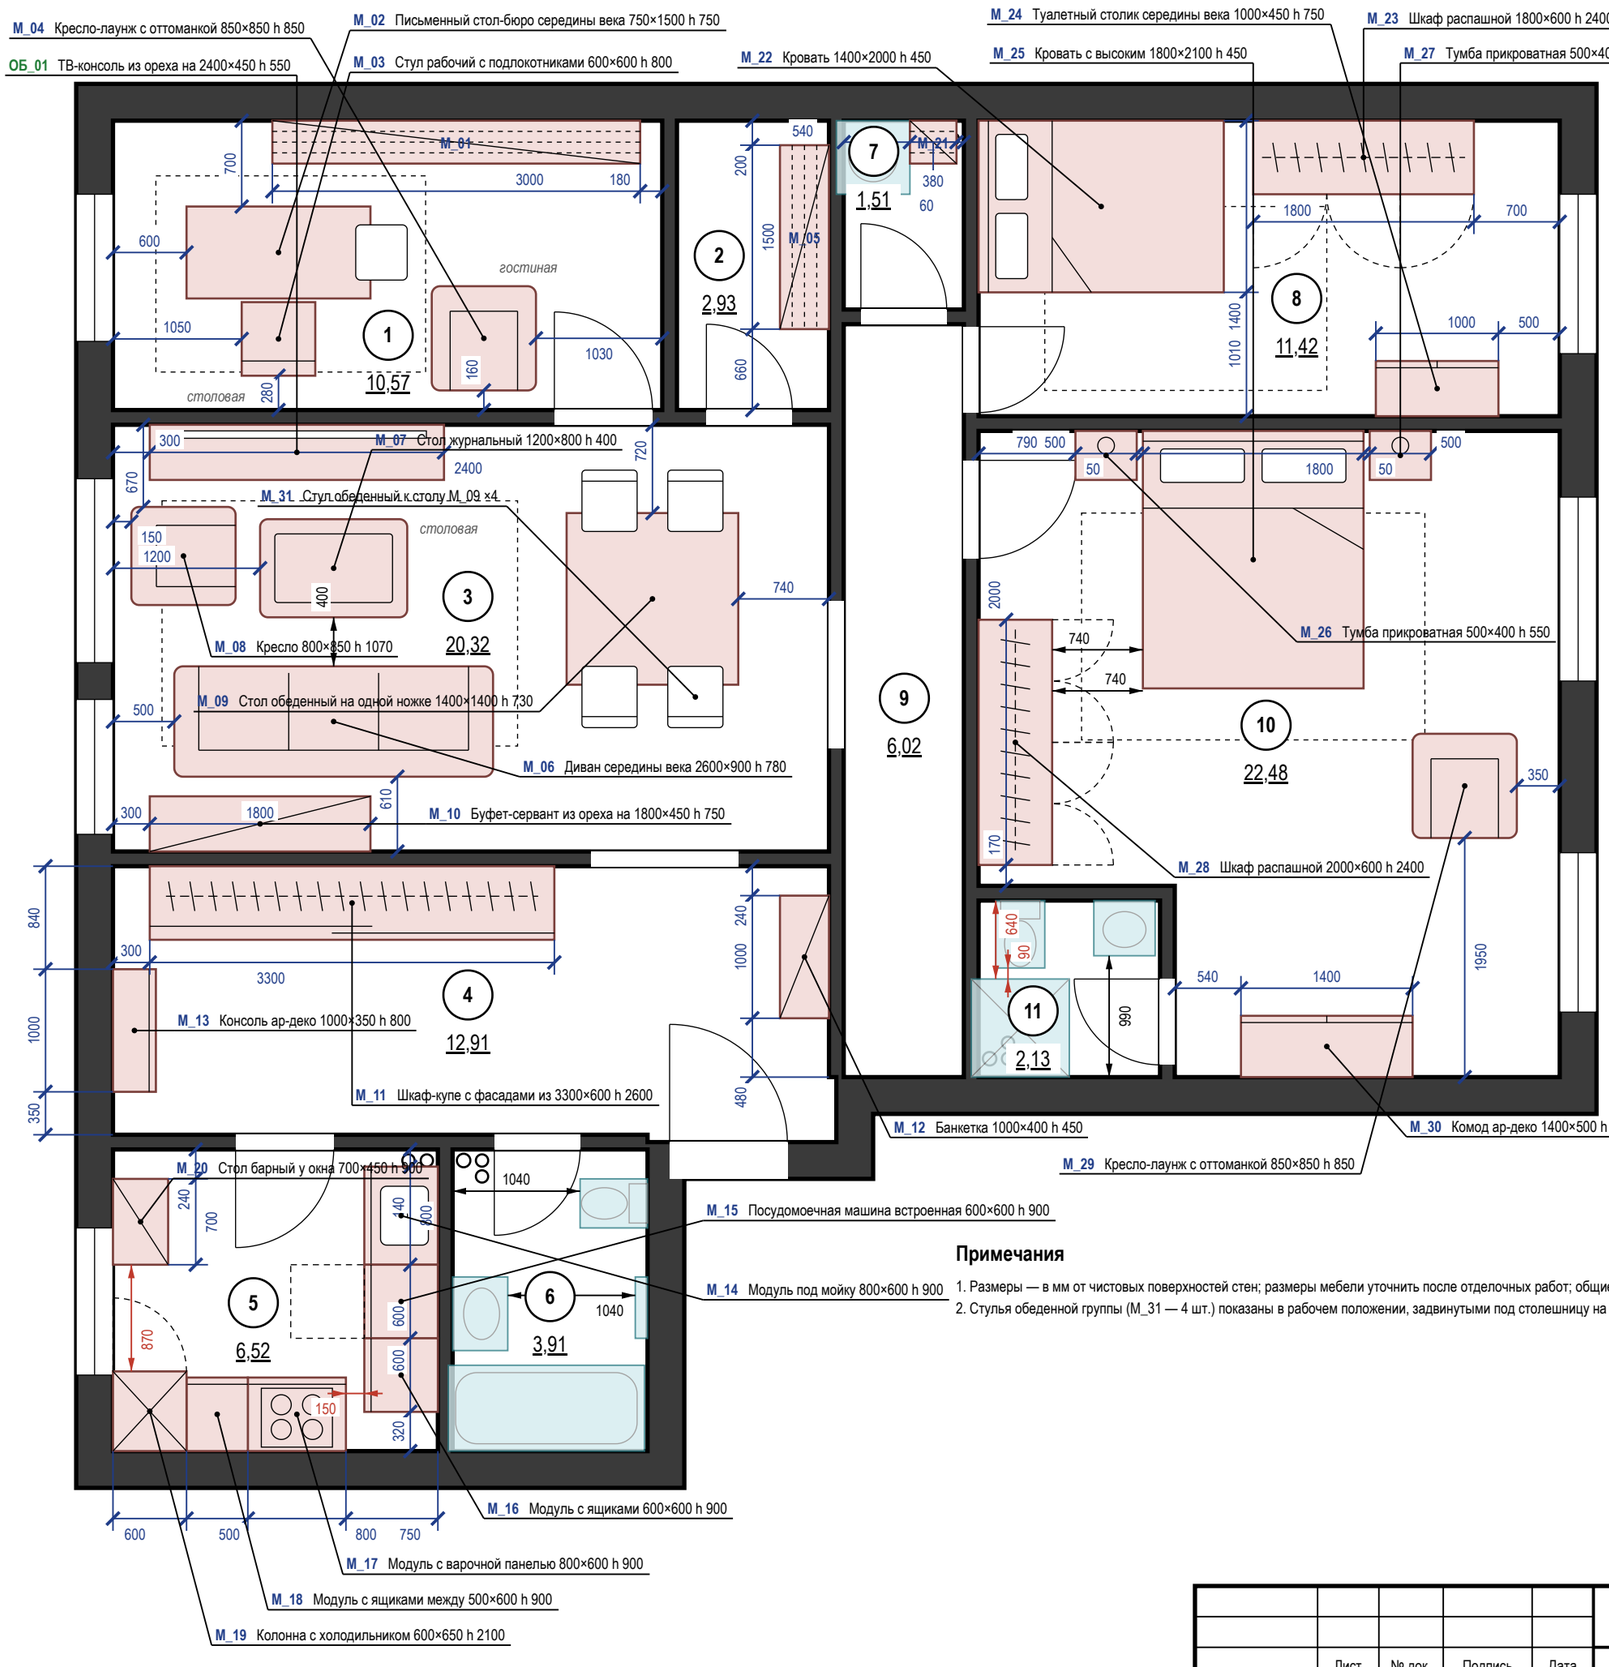

Экспликация помещений

лист обмерного плана · на плане — номера в марках

Ведомость мебели и оборудования

Марка	Наименование	Ш×Г×В, мм	Пом.	Кол.
М_01	Стеллаж-библиотека из ореха на	3000×350×2400	1	1
М_02	Письменный стол-бюро середины века	750×1500×750	1	1
М_03	Стул рабочий с подлокотниками	600×600×800	1	1
М_04	Кресло-лаунж с оттоманкой	850×850×850	1	1
М_05	Стеллаж для хранения	1500×400×2400	2	1
ОБ_01	ТВ-консоль из ореха на	2400×450×550	3	1
М_06	Диван середины века	2600×900×780	3	1
М_07	Стол журнальный	1200×800×400	3	1
М_08	Кресло	800×850×1070	3	1
М_09	Стол обеденный на одной ножке	1400×1400×730	3	1
М_10	Буфет-сервант из ореха на	1800×450×750	3	1
М_11	Шкаф-купе с фасадами из	3300×600×2600	4	1
М_12	Банкетка	1000×400×450	4	1
М_13	Консоль ар-деко	1000×350×800	4	1
М_14	Модуль под мойку	800×600×900	5	1
М_15	Посудомоечная машина встроенная	600×600×900	5	1
М_16	Модуль с ящиками	600×600×900	5	1
М_17	Модуль с варочной панелью	800×600×900	5	1
М_18	Модуль с ящиками между	500×600×900	5	1
М_19	Колонна с холодильником	600×650×2100	5	1
М_20	Стол барный у окна	700×450×900	5	1
М_21	Полки для хранения	380×350×2000	7	1
М_22	Кровать 1400×2000	1400×2000×450	8	1
М_23	Шкаф распашной	1800×600×2400	8	1
М_24	Туалетный столик середины века	1000×450×750	8	1
М_25	Кровать 1800×2100 с высоким	1800×2100×450	10	1
М_26	Тумба прикроватная	500×400×550	10	1
М_27	Тумба прикроватная	500×400×550	10	1
М_28	Шкаф распашной	2000×600×2400	10	1
М_29	Кресло-лаунж с оттоманкой	850×850×850	10	1
М_30	Комод ар-деко	1400×500×800	10	1
М_31	Стул обеденный к столу М_09	450×500×820	3	4

Ш — вдоль стены (изголовья), Г — от стены (длина кровати)

Материалы, модели, допуск замены — лист 11

Примечания

1. Размеры — в мм от чистовых поверхностей стен; размеры мебели уточнить после отделочных работ; общие указания — лист 2.
2. Стулья обеденной группы (М_31 — 4 шт.) показаны в рабочем положении, задвинутыми под столешницу на 150 мм.

					Проект: Квартира 103 м²
	Лист	№ док.	Подпись	Дата	План размещения мебели и оборудования
Дизайнер	Кырлан А.С.			18.10.26	Стадия: П; Лист: 10; Листов: 103

выпуск 18.10.2026 № d119044df4 · стр. 10 из 103

Поз.	Наименование и техническая характеристика	Тип, марка, обозначение документа, опросного листа	Код продукции	Поставщик	Ед. измерения	Кол.	Масса 1 ед., кг	Примечание
	Мебель встроенная и корпусная (изготовление по чертежам мебельщика)							
M_11	Шкаф-купе с фасадами из ореха и латунными профилями; корпус ЛДСП, фасады — матовая эмаль в цвет стен (Farrow & Ball No. 291); Ш×Г×В 3300×600×2600 мм			изготовление на заказ	шт.	1		пом. 4
M_14	Модуль под мойку, фасады — шпон ореха; корпус ЛДСП, фасады — матовая эмаль в тон стен; Ш×Г×В 800×600×900 мм			изготовление на заказ	шт.	1		пом. 5
M_15	Посудомоечная машина встроенная; корпус ЛДСП, фасады — матовая эмаль в тон стен; Ш×Г×В 600×600×900 мм			изготовление на заказ	шт.	1		пом. 5
M_16	Модуль с ящиками; корпус ЛДСП, фасады — матовая эмаль в тон стен; Ш×Г×В 600×600×900 мм			изготовление на заказ	шт.	1		пом. 5
M_17	Модуль с варочной панелью (индукция) и духовым шкафом; корпус ЛДСП, фасады — матовая эмаль в тон стен; Ш×Г×В 800×600×900 мм			изготовление на заказ	шт.	1		пом. 5
M_18	Модуль с ящиками между колонной и плитой; корпус ЛДСП, фасады — матовая эмаль в тон стен; Ш×Г×В 500×600×900 мм			изготовление на заказ	шт.	1		пом. 5
M_19	Колонна с холодильником, ретро-фасад цвета тил; корпус ЛДСП, фасады — матовая эмаль в тон стен; Ш×Г×В 600×650×2100 мм			изготовление на заказ	шт.	1		пом. 5
M_23	Шкаф распашной, орех, латунные ручки; корпус ЛДСП, фасады — матовая эмаль в цвет стен (Farrow & Ball No. 291); Ш×Г×В 1800×600×2400 мм			изготовление на заказ	шт.	1		пом. 8
M_28	Шкаф распашной, фасады — орех с латунными вставками; корпус ЛДСП, фасады — матовая эмаль в цвет стен (Farrow & Ball No. 291); Ш×Г×В 2000×600×2400 мм			изготовление на заказ	шт.	1		пом. 10
	Мебель покупная							
M_01	Стеллаж-библиотека из ореха на всю стену, латунные полкодержатели; шпон, дуб натуральный, матовое масло; Ш×Г×В 3000×350×2400 мм			аналог по характеристикам	шт.	1		пом. 1; замена ≤ габарита
M_02	Письменный стол-бюро середины века, орех, конические ножки; шпон, дуб натуральный, матовое масло; Ш×Г×В 750×1500×750 мм			аналог по характеристикам	шт.	1		пом. 1; замена ≤ габарита
M_03	Стул рабочий с подлокотниками, гнутая фанера и кожа; обивка — ткань, цвет Farrow & Ball No. 298; каркас — дуб натуральный; Ш×Г×В 600×600×800 мм			аналог по характеристикам	шт.	1		пом. 1; замена ≤ габарита
M_04	Кресло-лаунж с оттоманкой (в духе Eames Lounge Chair), палисандровый шпон, чёрная кожа; обивка — ткань, цвет Farrow & Ball No. 298; Ш×Г×В 850×850×850 мм			аналог по характеристикам	шт.	1		пом. 1; замена ≤ габарита
M_05	Стеллаж для хранения, орех; каркас и полки — ЛДСП, декор «дуб натуральный»; Ш×Г×В 1500×400×2400 мм			аналог по характеристикам	шт.	1		пом. 2; замена ≤ габарита
M_06	Диван середины века (в духе Florence Knoll), букле горчичного цвета, латунные опоры; обивка — ткань, цвет Farrow & Ball No. 298; Ш×Г×В 2600×900×780 мм			аналог по характеристикам	шт.	1		пом. 3; замена ≤ габарита
M_07	Стол журнальный (в духе Noguchi Coffee Table), орех и стекло; шпон, дуб натуральный, матовое масло; Ш×Г×В 1200×800×400 мм			аналог по характеристикам	шт.	1		пом. 3; замена ≤ габарита
M_08	Кресло (в духе Egg Chair), изумрудный бархат; обивка — ткань, цвет Farrow & Ball No. 298; Ш×Г×В 800×850×1070 мм			аналог по характеристикам	шт.	1		пом. 3; замена ≤ габарита
M_09	Стол обеденный на одной ножке (в духе Tulip Table), мрамор Calacatta, d 1400; шпон, дуб натуральный, матовое масло; Ш×Г×В 1400×1400×730 мм			аналог по характеристикам	шт.	1		пом. 3; замена ≤ габарита
M_10	Буфет-сервант из ореха на конических ножках, раздвижные двери; шпон, дуб натуральный, матовое масло; Ш×Г×В 1800×450×750 мм			аналог по характеристикам	шт.	1		пом. 3; замена ≤ габарита
M_31	Стул обеденный к столу M_09; обивка — ткань, цвет Farrow & Ball No. 298; каркас — дуб натуральный; Ш×Г×В 450×500×820 мм			аналог по характеристикам	шт.	4		пом. 3; замена ≤ габарита
ОБ_01	ТВ-консоль из ореха на конических ножках, ТВ на стене; шпон, дуб натуральный, матовое масло; Ш×Г×В 2400×450×550 мм			аналог по характеристикам	шт.	1		пом. 3; замена ≤ габарита
M_12	Банкетка, изумрудный бархат, латунные ножки; Ш×Г×В 1000×400×450 мм			аналог по характеристикам	шт.	1		пом. 4; замена ≤ габарита
M_13	Консоль ар-деко, чёрный лак и латунь; шпон, дуб натуральный, матовое масло; Ш×Г×В 1000×350×800 мм			аналог по характеристикам	шт.	1		пом. 4; замена ≤ габарита
M_20	Стол барный у окна, терраццо; Ш×Г×В 700×450×900 мм			аналог по характеристикам	шт.	1		пом. 5; замена ≤ габарита

Примечания

1. Позиции мебели совпадают с марками на плане расстановки; размеры Ш×Г×В — Ш вдоль стены, Г от стены.
2. Встроенная и корпусная мебель изготавливается по чертежам мебельщика после контрольного обмера; графы «Тип, марка» и «Код продукции» для неё не заполняются (ГОСТ 21.110-2013).
3. Покупные изделия — аналог по характеристикам: заменять только на изделия не больше указанного габарита и того же материала и цвета.
4. Материал и цвет, не указанные в данных изделия, приняты по концепции: тон дерева — по полу, обивка — по вторичному цвету палитры; образцы согласовать до заказа.
5. Масса 1 ед. для изделий до 25 кг не указывается. Техника — по монтажным схемам изготовителя; выводы — по листам ЭОМ и ВК.

					Проект: Квартира 103 м²
	Лист	№ док.	Подпись	Дата	Спецификация мебели и оборудования
Дизайнер	Кырлан А.С.			18.10.26	

Стадия	Лист	Листов
П	11	103

выпуск 18.10.2026 № d119044df4 · стр. 11 из 103

Поз.	Наименование и техническая характеристика	Тип, марка, обозначение документа, опросного листа	Код продукции	Поставщик	Ед. измерения	Кол.	Масса 1 ед., кг	Примечание
M_21	Полки для хранения; каркас и полки — ЛДСП, декор «дуб натуральный»; Ш×Г×В 380×350×2000 мм			аналог по характеристикам	шт.	1		пом. 7; замена ≤ габарита
M_22	Кровать 1400×2000, изголовье с каннелюрами, бархат цвета тил; мягкое изголовье, обивка — ткань, цвет Farrow & Ball No. 298; Ш×Г×В 1400×2000×450 мм			аналог по характеристикам	шт.	1		пом. 8; замена ≤ габарита
M_24	Туалетный столик середины века с круглым зеркалом; шпон, дуб натуральный, матовое масло; Ш×Г×В 1000×450×750 мм			аналог по характеристикам	шт.	1		пом. 8; замена ≤ габарита
M_25	Кровать 1800×2100 с высоким изголовьем ар-деко, изумрудный бархат, латунный кант; мягкое изголовье, обивка ткань, цвет Farrow & Ball No. 298; Ш×Г×В 1800×2100×450 мм			аналог по характеристикам	шт.	1		пом. 10; замена ≤ габарита
M_26, M_27	Тумба прикроватная, орех и латунь; шпон, дуб натуральный, матовое масло; Ш×Г×В 500×400×550 мм			аналог по характеристикам	шт.	2		пом. 10; замена ≤ габарита
M_29	Кресло-лаунж с оттоманкой (в духе Eames Lounge Chair), коньячная кожа; обивка — ткань, цвет Farrow & Ball No. 298; Ш×Г×В 850×850×850 мм			аналог по характеристикам	шт.	1		пом. 10; замена ≤ габарита
M_30	Комод ар-деко, макассар и латунь; шпон, дуб натуральный, матовое масло; Ш×Г×В 1400×500×800 мм			аналог по характеристикам	шт.	1		пом. 10; замена ≤ габарита
	Техника встраиваемая и бытовая, светильники под розетки							
	Посудомоечная машина встраиваемая, в модуле M_15; ниша 600 мм			аналог по характеристикам	шт.	1		пом. 5; по схеме изготовителя
	Варочная панель встраиваемая, электрическая, в модуле M_17			аналог по характеристикам	шт.	1		пом. 5; по схеме изготовителя
	Духовой шкаф встраиваемый, в модуле M_17			аналог по характеристикам	шт.	1		пом. 5; по схеме изготовителя
	Холодильник встраиваемый, в модуле M_19			аналог по характеристикам	шт.	1		пом. 5; по схеме изготовителя
	Вытяжка встраиваемая, над модулем M_14			аналог по характеристикам	шт.	1		пом. 5; вывод P21 (ЭОМ)
	Стиральная машина			аналог по характеристикам	шт.	1		пом. 6; вывод P7 (ЭОМ)
	Стиральная машина, место по листу ВК (ОБ_02); Ш×Г 600×600 мм			аналог по характеристикам	шт.	1		пом. 7; по схеме изготовителя
	Торшер, у поз. M_10; абажур — ткань или опаловое стекло; лампа 2700 K			аналог по характеристикам	шт.	1		пом. 3; розетка P3 (ЭОМ)
	Торшер, у поз. M_28; абажур — ткань или опаловое стекло; лампа 2700 K			аналог по характеристикам	шт.	1		пом. 10; розетка P5 (ЭОМ)
	Текстиль							
T7	Портьеры-волна; лён 100 %; цвет NCS S 1005-Y20R; карниз 1820 мм, высота 2610 мм, сборка 2			аналог по характеристикам	шт.	2		пом. 1
T8	Тюль; полиэстер 100 %; цвет NCS S 0502-Y; карниз 1820 мм, высота 2610 мм, сборка 2,5			аналог по характеристикам	шт.	1		пом. 1
T9	Ковёр под рабочей зоной, геометрия середины века; шерсть 100 %; цвет NCS S 2050-Y20R; 2200×1600 мм			аналог по характеристикам	шт.	1		пом. 1; с подложкой
T10	Подушки декоративные на кровать; букле (шерсть 60 %, полиэстер 40 %); цвет NCS S 3050-Y70R			аналог по характеристикам	шт.	3		пом. 1
T12	Плед на кровать; шерсть мериноса 100 %; цвет Farrow & Ball No. 289			аналог по характеристикам	шт.	1		пом. 1
T1	Портьеры-волна, два полотна; лён 100 %; цвет NCS S 1005-Y20R; карниз 2150 мм, высота 2690 мм, сборка 2			аналог по характеристикам	шт.	2		пом. 3
T2	Тюль-вуаль, одно полотно; полиэстер 100 %; цвет Farrow & Ball No. 291; карниз 2150 мм, высота 2690 мм, сборка 2,5			аналог по характеристикам	шт.	1		пом. 3
T3	Ковёр мягкой группы, абстрактная геометрия середины века; шерсть 100 %; цвет Farrow & Ball No. 298; 2900×2000 мм			аналог по характеристикам	шт.	1		пом. 3; с подложкой
T4	Подушки декоративные на диван; лён 100 %; цвет NCS S 1005-Y20R			аналог по характеристикам	шт.	3		пом. 3
T5	Подушки декоративные на диван, акцент; хлопковый бархат 100 %; цвет Farrow & Ball No. 255			аналог по характеристикам	шт.	2		пом. 3

					Проект: Квартира 103 м²
	Лист	№ док.	Подпись	Дата	Спецификация мебели и оборудования (продолжение)
Дизайнер	Кырлан А.С.			18.10.26	

Стадия	Лист	Листов
П	12	103

Поз.	Наименование и техническая характеристика	Тип, марка, обозначение документа, опросного листа	Код продукции	Поставщик	Ед. измерения	Кол.	Масса 1 ед., кг	Примечание
Т6	Плед на диван; шерсть мериноса 100 %; цвет Farrow & Ball No. 255			аналог по характеристикам	шт.	1		пом. 3
Т14	Рулонная штора кассетная, ткань димаут; полиэстер 100 %; цвет NCS S 1005-Y20R; карниз 890 мм, высота 1900 мм			аналог по характеристикам	шт.	1		пом. 5
Т11	Портьеры-волна; лён 100 %; цвет NCS S 1005-Y20R; карниз 1820 мм, высота 2610 мм, сборка 2			аналог по характеристикам	шт.	2		пом. 8
Т13	Тюль; полиэстер 100 %; цвет NCS S 0502-Y; карниз 1820 мм, высота 2610 мм, сборка 2,5			аналог по характеристикам	шт.	1		пом. 8
Т15	Ковёр под кроватью; шерсть 100 %; цвет NCS S 2050-Y20R; 2300×1500 мм			аналог по характеристикам	шт.	1		пом. 8; с подложкой
Т16	Подушки декоративные на кровать; букле (шерсть 60 %, полиэстер 40 %); цвет NCS S 3050-Y70R			аналог по характеристикам	шт.	3		пом. 8
Т17	Подушки на кровать, акцент; хлопковый бархат 100 %; цвет NCS S 5030-B10G			аналог по характеристикам	шт.	2		пом. 8
Т18	Плед на кровать; шерсть мериноса 100 %; цвет Farrow & Ball No. 289			аналог по характеристикам	шт.	1		пом. 8
Т19	Портьеры-волна; лён 100 %; цвет NCS S 1005-Y20R; карниз 2500 мм, высота 2610 мм, сборка 2			аналог по характеристикам	шт.	2		пом. 10
Т20	Тюль; полиэстер 100 %; цвет NCS S 0502-Y; карниз 2500 мм, высота 2610 мм, сборка 2,5			аналог по характеристикам	шт.	1		пом. 10
Т21	Ковёр под кроватью; шерсть 80 %, хлопок 20 %; цвет Farrow & Ball No. 298; 2800×1850 мм			аналог по характеристикам	шт.	1		пом. 10; с подложкой
Т22	Подушки декоративные на кровать; лён 100 %; цвет NCS S 1005-Y20R			аналог по характеристикам	шт.	3		пом. 10
Т23	Подушки на кровать, акцент; хлопковый бархат 100 %; цвет Farrow & Ball No. 289			аналог по характеристикам	шт.	2		пом. 10
Т24	Плед на кровать; шерсть мериноса 100 %; цвет Farrow & Ball No. 289			аналог по характеристикам	шт.	1		пом. 10
	Декор							
ДК3	Картина над креслом: графика середины века, рама — орех; 1000×700 мм; низ на 1100 мм от пола			аналог по характеристикам	шт.	1	4	пом. 1; крепление к стене
ДК1	Картина над буфетом: абстракция середины века, рама — латунь; 1200×900 мм; низ на 1000 мм от пола			аналог по характеристикам	шт.	1	6	пом. 3; крепление: планка на дюбелях, 4 точки
ДК2	Фикус лировидный в кашпо Ø400; 450×450 мм			аналог по характеристикам	шт.	1		пом. 3
ДК5	Зеркало; рама — чёрный матовый; 800×1800 мм; низ на 550 мм от пола			аналог по характеристикам	шт.	1	18	пом. 4; крепление: анкер, 4 шт.
ДК8	Часы настенные Ø400; 400×400 мм; центр на 1550 мм от пола			аналог по характеристикам	шт.	1	2	пом. 5; крепление: дюбель с крюком, 1 точка
ДК9	Хлорофитум хохлатый на подоконнике (отм. +0,800); 300×200 мм; низ на 800 мм от пола			аналог по характеристикам	шт.	1		пом. 5
ДК4	Картина над кроватью: графика в паспарту, рама — дуб; 1000×700 мм; низ на 1100 мм от пола			аналог по характеристикам	шт.	1	4	пом. 8; крепление к стене
ДК6	Зеркало в рост в тонкой чёрной раме; рама — чёрный матовый; 600×1600 мм; низ на 300 мм от пола			аналог по характеристикам	шт.	1	12	пом. 8; крепление: анкер для пустотелых оснований, 4 шт.
ДК7	Картина над кроватью: абстракция, холст, тонкая рама из дуба; 1200×700 мм; низ на 1300 мм от пола			аналог по характеристикам	шт.	1	4	пом. 10; крепление к стене

					Проект: Квартира 103 м²		
	Лист	№ док.	Подпись	Дата	Спецификация мебели и оборудования (продолжение)	Стадия	Лист	Листов
Дизайнер	Кырлан А.С.			18.10.26		П	13	103

Ведомость изделий

Марка	Наименование	Пом.	Ш×Г×В, мм	Корпус	Фасад	Кромка, мм скр./вид.	Кол.
M_05	Система хранения	2	1500×400×2400	ЛДСП 16	без фасадов; ящики — МДФ 18, эмаль матовая	0,4 / 2	1
M_11	Шкаф-купе	4	3300×600×2600	ЛДСП 16	рифлёные панели МДФ в алюминиевом профиле	0,4 / 2	1
M_21	Система хранения	7	380×350×2000	ЛДСП 16	без фасадов; ящики — МДФ 18, эмаль матовая	0,4 / 2	1
M_23	Шкаф распашной	8	1800×600×2400	ЛДСП 16	МДФ 18, эмаль матовая	0,4 / 2	1
M_28	Шкаф распашной	10	2000×600×2400	ЛДСП 16	МДФ 18, эмаль матовая	0,4 / 2	1
M_14	Модуль нижний: мойка	5	800×600×900	ЛДСП 16	МДФ 18, эмаль матовая	0,4 / 2	1
M_15	Модуль нижний: ПММ	5	600×600×900	ЛДСП 16	МДФ 18, эмаль матовая	0,4 / 2	1
M_16	Модуль нижний: ящики	5	600×600×900	ЛДСП 16	МДФ 18, эмаль матовая	0,4 / 2	1
M_17	Модуль нижний: духовой шкаф, варочная	5	800×600×900	ЛДСП 16	МДФ 18, эмаль матовая	0,4 / 2	1
M_18	Модуль нижний: ящики	5	500×600×900	ЛДСП 16	МДФ 18, эмаль матовая	0,4 / 2	1
M_19	Пенал: холодильник встр.	5	600×650×2100	ЛДСП 16	МДФ 18, эмаль матовая	0,4 / 2	1

Ведомость встраиваемой техники

Поз.	Прибор	Ниша, вырез, мм	Вентиляция	Питание	Схема
M_14	Мойка врезная / подстольная с сифоном	вырез по шаблону, ориентир 700 × 480		смеситель — выводы ВК	по модели
M_15	Посудомоечная машина встраиваемая, 60 см	ниша 600 × 862 (от пола до низа столешницы)	зазор в цоколе, по схеме	розетка в соседнем модуле	по модели
M_17	Духовой шкаф встраиваемый, 60 см	ниша 560 × 595, глубина ≥ 550	зазор за шкафом, вырез в задней стенке	вывод кабеля под шкафом	по модели
M_17	Варочная панель индукционная, 60 см	вырез в столешнице 560 × 490		вывод кабеля под модулем	по модели
M_19	Холодильник встраиваемый, ниша 1780	ниша 1780 × 560 × 550	решётка в цоколе, канал за корпусом, выход сверху	розетка над нишей или в соседнем модуле	по модели
M_17	Вытяжка настенная, 60 см	низ ≥ 650 над панелью	воздуховод к вентканалу, короб до потолка	вывод кабеля в коробе	по модели

Ведомость фурнитуры

№	Фурнитура	Тип, размер	Изделия	Кол.
1	Полкодержатель с фиксацией	ø5 мм	M_05, M_11, M_23, M_28, M_19	132
2	Штанга выдвижная торцевая	L по глубине	M_05, M_21	2
3	Опора регулируемая с цоколем на клипсах	ход 20 мм	M_05, M_11, M_21, M_23, M_28	38
4	Анкер по основанию стены	по таблице крепежа	M_05, M_11, M_21, M_23, M_28	30
5	Уголок крепления к стене от опрокидывания	стальной	M_05, M_11, M_21, M_23, M_28, M_19	12
6	Система дверей купе: профиль, направляющие, ролики	на 4 двери	M_11	1
7	Ручка-профиль вертикальная	в цвет профиля	M_11	4
8	Штанга овальная 30×15, L = 817	+ 2 держателя	M_11	1
9	Полка для обуви выдвижная наклонная	ширина 817	M_11	3
10	Полка для обуви выдвижная наклонная	ширина 794	M_11	3
11	Штанга овальная 30×15, L = 794	+ 2 держателя	M_11	1
12	Петля накладная 110° с доводчиком	чашка 35 мм	M_23, M_28, M_14, M_19	59
13	Штанга овальная 30×15, L = 876	+ 2 держателя	M_23	1
14	Штанга овальная 30×15, L = 976	+ 2 держателя	M_28	1
15	Ручка-профиль	латунь матовая	M_14, M_15, M_16, M_17, M_18, M_19	13
16	Опора кухонная регулируемая 100–120 мм	+ клипса цоколя	M_14, M_15, M_16, M_17, M_18, M_19	28
17	Комплект навески фасада ПММ	из поставки машины	M_15	1
18	Направляющие полного выдвижения с доводчиком NL 500	пара	M_16, M_17, M_18	7

Примечания


1. Модели техники выбирает заказчик до изготовления мебели; ниши, вырезы и вентиляция — по монтажной схеме выбранной модели (условие гарантии), её номер вносится в ведомость.
2. Количество фурнитуры — по чертежам изделий; запас крепежа 5 %. Аналоги — по характеристикам (доводчик, нагрузка, ход).
3. Цвет корпусов, фасадов и профилей — по колерной карте проекта.

					Проект: Квартира 103 м²
	Лист	№ док.	Подпись	Дата	Ведомости изделий, техники и фурнитуры
Дизайнер	Кырлан А.С.			18.10.26	


Стадия	Лист	Листов
П	14	103

выпуск 18.10.2026 № d119044df4 · стр. 14 из 103


Фрагмент 1. Ванная (пом. 6)

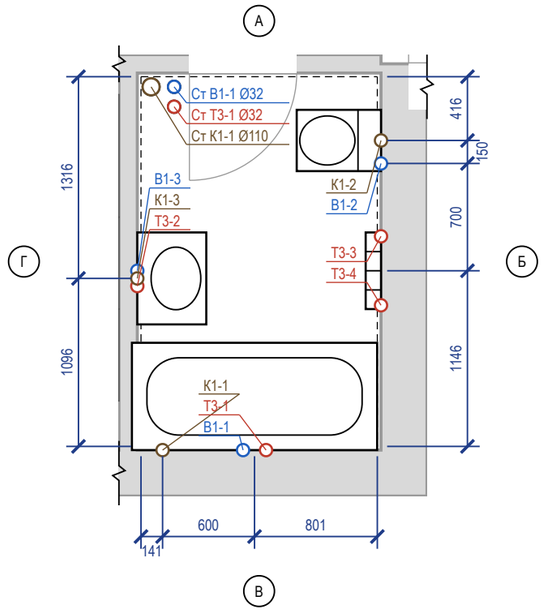


Фрагмент 2. Постирочная (пом. 7)

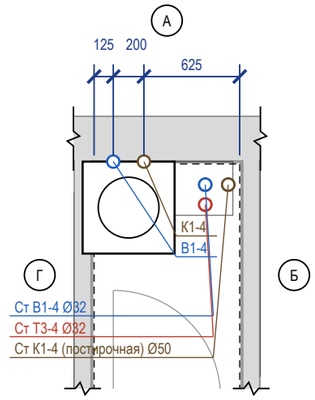

Фрагмент 3. Ванная мастер (пом. 11)

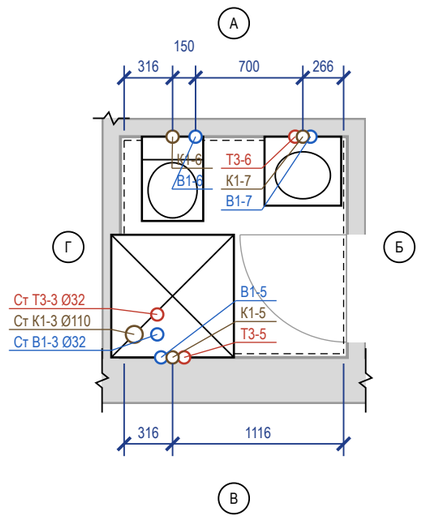

Фрагмент 4. Кухня (пом. 5)

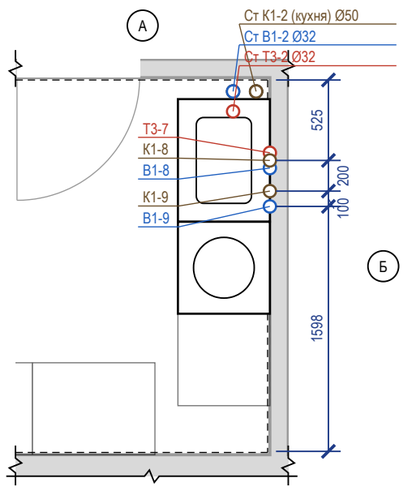

Ведомость привязок выводов

Код	Прибор	Ø	H, мм	Привязка от чист. стен, мм	Прим.
В1-1	С_01 ванна	½"	800	ст. В: 666 от Г	межос. 150
Т3-1	С_01 ванна	½"	800	ст. В: 726 от Б	межос. 150
К1-1	С_01 ванна	Ø50	50	ст. В: 141 от Г	
В1-2	С_02 унитаз подвесной	½"	250	ст. Б: 566 от А	в раме инсталляции
К1-2	С_02 унитаз подвесной	Ø110	220	ст. Б: 416 от А	
В1-3	С_03 умывальник	½"	600	ст. Г: 1146 от В	межос. 100
Т3-2	С_03 умывальник	½"	600	ст. Г: 1046 от В	межос. 100
К1-3	С_03 умывальник	Ø50	500	ст. Г: 1096 от В	
Т3-3	С_04 полотенцесушитель	½"	1150	ст. Б: 1041 от А	подача, межос. 450; байпас и краны
Т3-4	С_04 полотенцесушитель	½"	1150	ст. Б: 921 от В	обратка
В1-4	ОБ_02 стиральная машина	½"	600	ст. А: 125 от Г	кран машины
К1-4	ОБ_02 стиральная машина	Ø50	600	ст. А: 325 от Г	
В1-5	С_05 душ	½"	1200	ст. В: 241 от Г	межос. 150
Т3-5	С_05 душ	½"	1200	ст. В: 391 от Г	межос. 150
К1-5	С_05 душ	Ø50	70	ст. В: 316 от Г	сифон поддона
В1-6	С_06 унитаз подвесной	½"	250	ст. А: 466 от Г	в раме инсталляции
К1-6	С_06 унитаз подвесной	Ø110	220	ст. А: 316 от Г	
В1-7	С_07 умывальник	½"	600	ст. А: 216 от Б	межос. 100
Т3-6	С_07 умывальник	½"	600	ст. А: 316 от Б	межос. 100
К1-7	С_07 умывальник	Ø50	500	ст. А: 266 от Б	
В1-8	П9 мойка кухонная	½"	600	ст. Б: 575 от А	межос. 100
Т3-7	П9 мойка кухонная	½"	600	ст. Б: 475 от А	межос. 100
К1-8	П9 мойка кухонная	Ø50	400	ст. Б: 525 от А	
В1-9	П10 посудомоечная машина	½"	550	ст. Б: 825 от А	кран ПММ в шкафу мойки
К1-9	П10 посудомоечная машина	Ø40	550	ст. Б: 725 от А	слив ПММ в шкафу мойки

Условные обозначения

- вывод В1 (код — в ведомости привязок)
- вывод Т3 (код — в ведомости привязок)
- вывод К1 (код — в ведомости привязок)
- сантехприбор по расстановке (габарит модели)
- чистовая поверхность стены (от неё привязки)
- стояк «Ст К1-N / Ст В1-N» (ГОСТ 21.601), Ø мм
- линия обрыва (граница фрагмента)
- А — обозначение стены А–Г (как на развёртках)


Примечания

1. Привязки выводов даны от чистовых поверхностей стен (облицовка на сторону: ванная — 24 мм (штукатурка 10 + клей 5 + плитка 9); постирочная — 15 мм (штукатурка 10 + шпаклёвка 5 (принято)); ванная мастер — 24 мм (штукатурка 10 + клей 5 + плитка 9); кухня — 22 мм (фартук: штукатурка 10 + клей 3 + плитка 9)); эти же грани — на развёртках и в раскладке плитки. Высоты — от чистого пола помещения.
2. До черновой разводки сверить по паспорту выбранного прибора (смеситель, инсталляция, сифон).
3. Горячая вода (Т3) — слева от холодной (В1), если смотреть на прибор. Допуск установки выводов: ±5 мм в группе, ±20 мм у отдельно стоящих.
4. Расчёт систем водоснабжения и канализации и подбор оборудования выполняет проектная организация; лист задаёт места и высоты выводов.
5. Посудомоечная машина П10: кран и слив — отдельными выводами в шкафу мойки (не за машиной), до машины ≤ 1500 мм.
6. Прибор П9 мойка кухонная, П10 посудомоечная машина взят из расстановки мебели (по шкафу с мойкой).


					Проект: Квартира 103 м²
	Лист	№ док.	Подпись	Дата	
Дизайнер	Кырлан А.С.			18.10.26	План выводов сантехники
					Стадия: П; Лист: 15; Листов: 103

выпуск 18.10.2026 № d119044df4 · стр. 15 из 103


План квартиры (М 1:200)

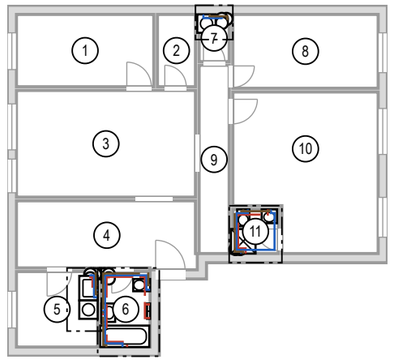


Фр. 2. Постирочная (М 1:25)

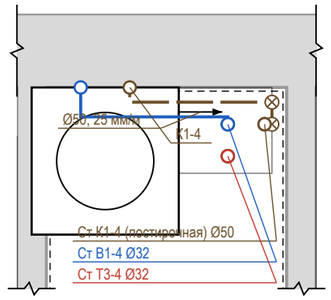


Фр. 1. Ванная (М 1:25)

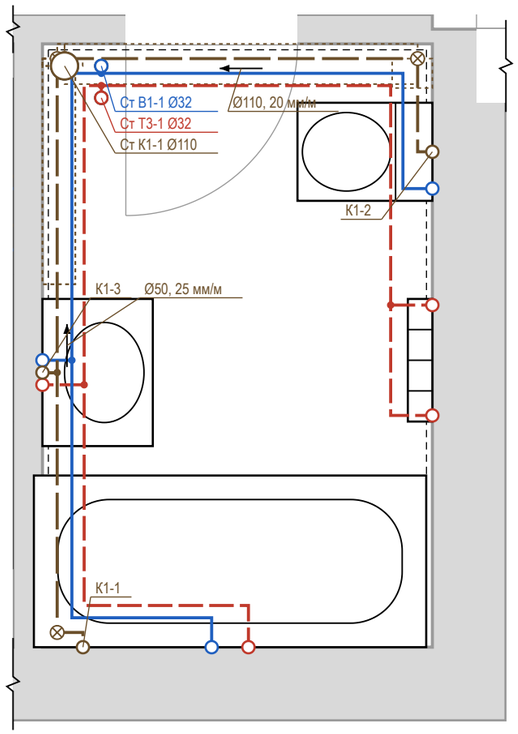

Фр. 3. Ванная мастер (М 1:25)

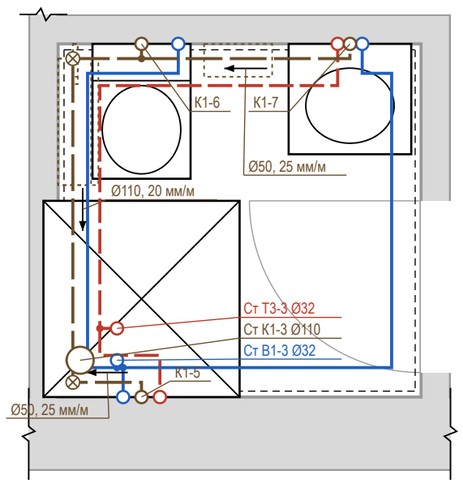

Фр. 4. Кухня (М 1:25)

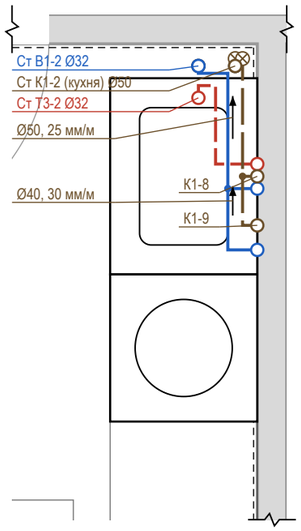

Условные обозначения


- В1 — водопровод хозяйственно-питьевой (ХВС), PP-R Ø20
- Т3 — горячее водоснабжение, подача (ГВС), PP-R Ø20
- К1 — канализация бытовая
- направление уклона К1 / пола: Ø, мм на 1 м
- ревизия (прочистка) К1 — доступ сохранить
- тройник (ответвление к прибору)
- короб К1 над чистым полом (ГКЛВ под плитку)
- вывод В1 (код — в ведомости привязок)
- вывод Т3 (код — в ведомости привязок)
- вывод К1 (код — в ведомости привязок)
- сантехприбор по расстановке (габарит модели)
- стояк «Ст К1-N / Ст В1-N» (ГОСТ 21.601), Ø мм
- линия обрыва (граница фрагмента)
- граница фрагмента на плане (Фр. N)

Профиль выпусков К1 (до врезки в стояк)

Выпуск	Прибор	Ø	L, м	i, мм/м	Δh, мм	Прокладка, мм
К1-2	С_02 унитаз подвесной	Ø110	1,91	20	38	под дверью — перенести выпуск
К1-6	С_06 унитаз подвесной	Ø110	1,60	20	32	короб 180×140
К1-1	С_01 ванна	Ø50	2,56	25	64	короб 150×110
К1-7	С_07 умывальник	Ø50	2,45	25	61	короб 150×110
К1-3	С_03 умывальник	Ø50	1,40	25	35	короб 120×110
К1-4	ОБ_02 стиральная машина	Ø50	0,76	25	19	над полом за приборами
К1-8	П9 мойка кухонная	Ø50	0,60	25	15	в полу, стяжка ≥ 110
К1-5	С_05 душ	Ø50	0,46	25	12	над полом за приборами
К1-9	П10 посудомоечная машина	Ø40	0,80	30	24	в полу, стяжка ≥ 109

Короб h×b: h — от чистого пола, b — от чистовой стены. Стяжка 35 мм — лист полов.

Узел ввода В1, Т3 (схема, без масштаба)

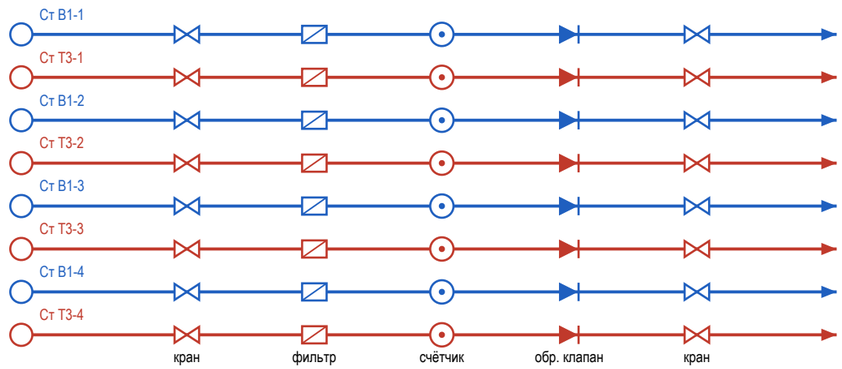

⊗ Ст К1-1, Ст К1-2 (кухня), Ст К1-3, Ст К1-4 (постирочная): ревизия на стояке — люк в коробе

Примечания

1. Трассы принципиальные, построены от стояков вдоль стен помещений; фактическое положение фиксируется исполнительной схемой с привязками (фото с рулеткой) до закрытия.
2. Уклон К1 не менее 1/d и не более 150 мм/м (СП 30.13330.2020, п. 19.1), приняты практические уклоны; поворот — двумя отводами 45°, ревизия после поворота, доступ сохранить. Стояк К1 в коробе — звукоизоляция стояка в коробе, без жёсткого контакта короба с трубой.
3. Решение по К1: стяжка 35 мм не укрывает трубы (нужно Ø + Δh + 45 мм) — выпуски идут над чистым полом вдоль стен: К1-4, К1-5 — за приборами и в раме инсталляции; К1-2, К1-6, К1-1, К1-7, К1-3 — в коробе ГКЛВ под плитку (размеры в профиле). Короба — на развёртках; отметку низа врезки в стояк замерить до черновых работ.
4. Трасса К1 от К1-2 проходит под дверным проёмом — короб там невозможен: выпуск перенести или вести в полу с подъёмом пола помещения.
5. На каждом вводе В1 и Т3 — кран шаровой, фильтр, счётчик, обратный клапан; доступ через люк не меньше 300×400. Водопровод — в штробе стен или в коробах; трубы испытать давлением до закрытия (акт скрытых работ).
6. Расчёт систем, диаметры магистралей и подбор оборудования выполняет проектная организация; врезка и перенос стояков — по согласованию с управляющей организацией. Арматуру и привязки сверить по паспортам приборов.

					Проект: Квартира 103 м²
	Лист	№ док.	Подпись	Дата	
Дизайнер	Кырлан А.С.			18.10.26	Схема разводки водопровода и канализации
					Стадия: П; Лист: 16; Листов: 103

выпуск 18.10.2026 № d119044df4 · стр. 16 из 103


Поз.	Наименование и техническая характеристика	Тип, марка, обозначение документа	Код продукции	Поставщик	Ед. изм.	Кол.	Масса 1 ед., кг	Примечание
	Санитарные приборы							
1	Ванна акриловая 1600×700 мм, с каркасом, экраном и отверстием слив-перелив	аналог		выбор заказчика	шт	1		С_01
2	Унитаз подвесной безободковый, с сиденьем микролифт, крепёж и звукоизолирующая прокладка	Jacob Delafon Struktura EDF102-00		выбор заказчика	шт	2		С_02, С_06
3	Инсталляция для подвесного унитаза: рама высотой 1120 мм, бачок, клавиша смыва (ось клавиши 1050 мм от чистого пола)	аналог		выбор заказчика	шт	2		С_02, С_06; короб ГКЛВ
4	Умывальник подвесной 600×450 мм, с отверстием под смеситель и переливом	аналог		выбор заказчика	шт	1		С_03
5	Умывальник подвесной 500×450 мм, с отверстием под смеситель и переливом	аналог		выбор заказчика	шт	1		С_07
6	Поддон душевой низкий 800×800 мм, с сифоном и выпуском Ø50, на ножках/подиуме	аналог		выбор заказчика	шт	1		С_05
7	Мойка кухонная 600×800 мм, с переливом	аналог		с кухонной мебелью	шт	1		П9
8	Полотенцесушитель водяной (ГВС), с байпасом и кранами	аналог		выбор заказчика	шт	1		С_04
	Смесители, сифоны и арматура приборов							
9	Смеситель для ванны настенный однорычажный, межосевое 150 мм, с душевым набором (лейка, шланг, держатель)	аналог		выбор заказчика	шт	1		С_01
10	Смеситель для умывальника однорычажный, с донным клапаном	аналог		выбор заказчика	шт	2		С_03, С_07
11	Душевая система скрытого монтажа с термостатом: встраиваемая часть, верхний душ, ручная лейка	аналог		выбор заказчика	шт	1		С_05; встраиваемая часть — до плитки
12	Смеситель кухонный однорычажный, высокий излив	аналог		выбор заказчика	шт	1		П9
13	Обвязка ванны слив-перелив Ø40/50 с сифоном	аналог		выбор заказчика	шт	1		С_01
14	Сифон для умывальника бутылочный Ø32/40–50, с гофрой к выпуску	аналог		выбор заказчика	шт	2		С_03, С_07
15	Сифон для мойки с отводом для ПММ Ø40/50	аналог		выбор заказчика	шт	1		П9
16	Сифон для стиральной машины встраиваемый в стену Ø50, с обратным клапаном	аналог		выбор заказчика	шт	1		ОБ_02
17	Кран угловой ½"×½" с гибкой подводкой 40 см (умывальники, мойка)	аналог		выбор заказчика	шт	6		по 2 на прибор
18	Кран шаровой угловой ½"×¾" для подключения стиральной и посудомоечной машины	аналог		выбор заказчика	шт	2		ОБ_02, П10
19	Узел подключения полотенцесушителя: байпас Ду20, краны шаровые ½" ×2	аналог		выбор заказчика	шт	1		
	Трубопроводы							
20	Труба полипропиленовая PP-R PN20 Ø20×3,4 (В1)	ГОСТ 32415-2013		выбор заказчика	м	19	0,17	11,4 + 5,5 + 10 %
21	Труба PP-R, армированная стекловолокном, PN20 Ø20×2,8 (Т3)	ГОСТ 32415-2013		выбор заказчика	м	17,5	0,15	9,4 + 6,1 + 10 %
22	Труба канализационная ПП Ø40 (К1)	ГОСТ 32414-2013		выбор заказчика	м	1		0,3 + 0,6 + 10 %
23	Труба канализационная ПП Ø50 (К1)	ГОСТ 32414-2013		выбор заказчика	м	8,5		5,3 + 2,1 + 10 %
24	Труба канализационная ПП Ø110 (К1)	ГОСТ 32414-2013		выбор заказчика	м	4,5		3,5 + 0,4 + 10 %
	Фасонные части и выводы							
25	Отвод канализационный ПП 45° Ø40	ГОСТ 32414-2013		выбор заказчика	шт	2		2 шт. на поворот
26	Отвод канализационный ПП 45° Ø50	ГОСТ 32414-2013		выбор заказчика	шт	24		2 шт. на поворот
27	Отвод канализационный ПП 45° Ø110	ГОСТ 32414-2013		выбор заказчика	шт	12		2 шт. на поворот
28	Тройник канализационный ПП 45° (врезки ветвей)	ГОСТ 32414-2013		выбор заказчика	шт	8		
29	Ревизия канализационная ПП (после поворота трассы)	ГОСТ 32414-2013		выбор заказчика	шт	11		доступ сохранить
30	Фитинги PP-R Ø20: тройники, угольники 90° (ветви и повороты В1, Т3)	ГОСТ 32415-2013		выбор заказчика	шт	46		
31	Водорозетка PP-R Ø20×½" настенная, с креплением	ГОСТ 32415-2013		выбор заказчика	шт	16		коды — лист выводов
	Узлы ввода, люки, короба							
32	Кран шаровой латунный Ду15 PN16 (отключение ввода)	аналог		выбор заказчика	шт	8		Ст В1-1, Ст Т3-1, Ст В1-2, Ст Т3-2, Ст В1-3, Ст Т3-3, Ст В1-4, Ст Т3-4
33	Фильтр сетчатый косой Ду15	аналог		выбор заказчика	шт	8		
34	Счётчик воды крыльчатый Ду15 (ХВ, ГВ), с поверкой	аналог		выбор заказчика	шт	8		пломба УК
35	Клапан обратный Ду15	аналог		выбор заказчика	шт	8		
36	Люк ревизионный нажимной под плитку 300×400 мм	аналог		выбор заказчика	шт	4		к стоякам и арматуре
37	Звукоизоляция стояка К1 в коробе: рулонный звукоизоляционный материал ≥ 10 мм, обмотка стояка на высоту этажа	аналог		выбор заказчика	м	10,8		Ст К1-1, Ст К1-2 (кухня), Ст К1-3, Ст К1-4 (постирочная)
38	Короб К1 над полом: профиль ПН/ПС, ГКЛВ 12,5 мм под плитку	аналог		выбор заказчика	м	5,4		сечение — лист разводки

Примечания

1. Форма 1 ГОСТ 21.110-2013, ширины граф изменены по п. 4.1. «Аналог» — аналог по характеристикам: модели внести до черновых работ, привязки выводов сверить по паспортам.
2. Бытовая техника не входит (показана арматура подключения), мойка — в комплекте кухни. Длины труб — трасса листа разводки + подъёмы + 10 %.
3. Стояк К1 в коробе — звукоизоляция стояка в коробе без жёсткого контакта короба с трубой.
4. Расчёт систем водоснабжения и канализации, диаметры магистралей и подбор оборудования выполняет проектная организация.

					Проект: Квартира 103 м²			
	Лист	№ док.	Подпись	Дата	Спецификация сантехнического оборудования	Стадия	Лист	Листов
Дизайнер	Кырлан А.С.			18.10.26		П	17	103

выпуск 18.10.2026 № d119044df4 · стр. 17 из 103

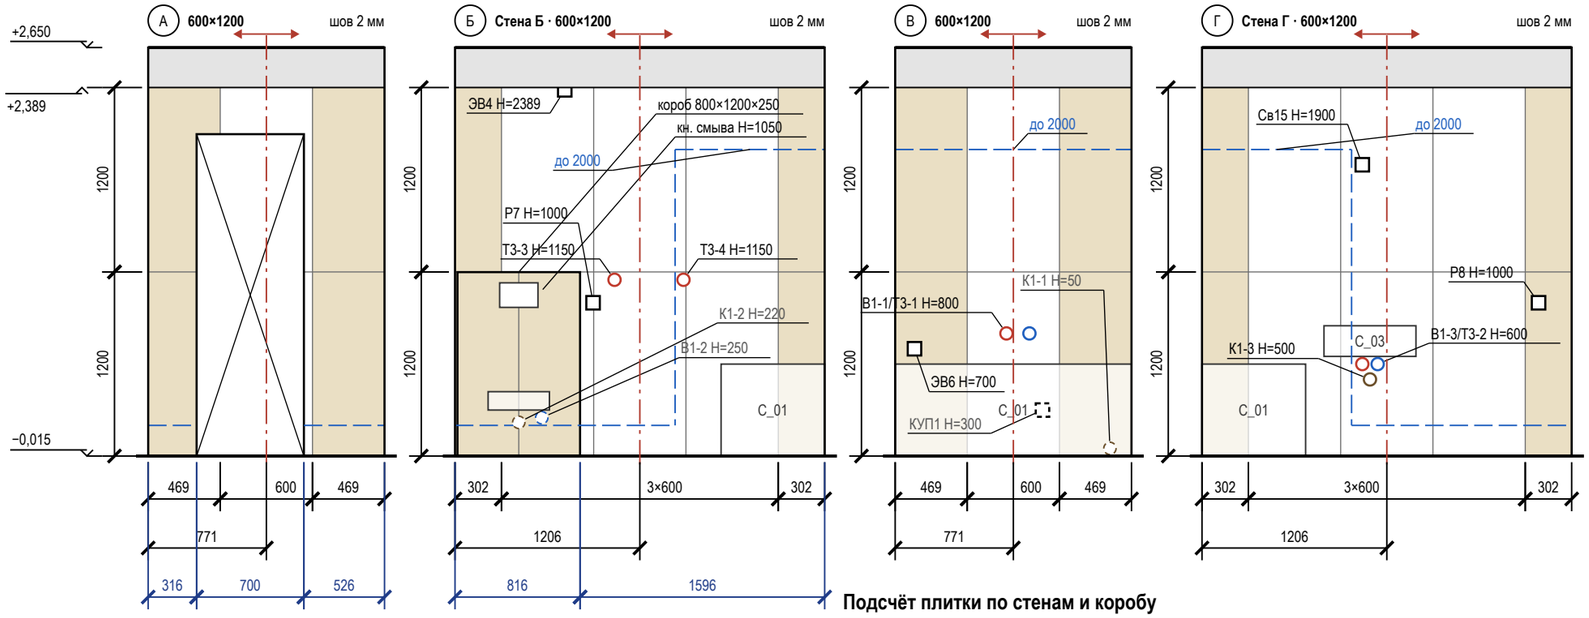

Подсчёт плитки по стенам и коробу

Поверхность	L × H, мм	S, м²	Целых	Подр.	С запасом	Подрезки: край / верх, мм
стена А	1542 × 2404	2,35	0	6	7	469 / 469; целый ряд
стена Б	2412 × 2404	4,95	5	5	11	302 / 302; целый ряд
короб (ст. Б)	800×1200×250	1,76	0	6	7	лицо 399 / 399; бок. 250
стена В	1542 × 2404	3,82	2	4	7	469 / 469; целый ряд
стена Г	2412 × 2404	5,91	6	4	11	302 / 302; целый ряд
Итого		**18,80**	**13**	**25**	**43**	

Сдвиг точек под раскладку

Точка (ВК, ЭОМ)	Стена	Проект: от угла / H	Под раскладку: от угла / H	Сдвиг, мм
Т3-3	Б	1041 / 1150	905 / 1150	−136 на шов
Т3-4	Б	1491 / 1150	1507 / 1150	+16 на шов
ЭВ4	Б	716 / 2389	604 / 2403	−112 в центр плитки; H +14
В1-1/Т3-1	В	801 / 800	771 / 800	−30 в центр плитки
ЭВ6	В	126 / 700	169 / 700	+43 в центр плитки
В1-3/Т3-2, К1-3	Г	1096 / 600, 500	1206 / 600, 500	+110 в центр плитки
Р8	Г	2196 / 1000	2109 / 1000	−87 на шов
Св15	Г	1046 / 1900	905 / 1900	−141 на шов

Условные обозначения

- плитка целая; тонкая линия — шов
- плитка с подрезкой (размер — на цепочке)
- ось старта; стрелки — направление укладки
- верх гидроизоляции: 200 от ЧП, в мокрой зоне — «до …»
- проём — не облицовывается
- сантехприбор: габарит, высота по практике
- короб инсталляции, в нём кнопка смыва 250×160
- вывод В1 (код — в ведомости привязок)
- вывод Т3 (код — в ведомости привязок)
- вывод К1 (код — в ведомости привязок)
- вывод за прибором / в коробе (не на сетке)
- электроточка: марка и H — по листам ЭОМ
- отметка уровня, м: ±0,000 — чистый пол жилых помещений
- низ потолка; серая полоса — стена без плитки
- А обозначение стены А–Г (как на развёртках)


Примечания

1. Вид изнутри, стены по часовой стрелке А → Г. Высоты — от чистого пола (−0,015), отметки — от ±0,000. Раскладка от чистовых размеров (штукатурка 10 + клей 5 + плитка 9 мм), подрезки чистые; старт — от оси стены, ряды от пола целыми.
2. Верх плитки +2,389, потолок +2,650, зазор 261 мм: потолок ГКЛ опустить до +2,392 (шов 3 мм, герметик) — согласовать с монтажником ГКЛ; иначе профиль-окантовка, полосу окрасить в цвет потолка. Подрезной ряд 256 мм не делать.
3. Точки из таблицы сдвигов переносятся до черновой разводки: смеситель — по оси пары В1 + Т3; вывод на оси прибора — вместе с прибором, иначе старт раскладки — на ось прибора.
4. За приборами и в коробе (В1-2, К1-2, К1-1, КУП1) — штриховым кольцом.
5. Гидроизоляция: 200 мм от ЧП по периметру; над ванной — до 2000 и 300 мм за борт (СП 29.13330.2011, п. 7.2 — на высоту замачивания); углы — лентой; акт скрытых работ, пролив.
6. Короб 800×1200×250: лицо 399 / 399 мм от оси кнопки смыва, боковины, полка; углы — запил 45° или профиль; за коробом плитку не кладут.
7. Между коробом и углом полоса 16 мм — довести короб до угла.

					Проект: Квартира 103 м²
	Лист	№ док.	Подпись	Дата	Раскладка плитки. Ванная. Развёртки стен
Дизайнер	Кырлан А.С.			18.10.26	

Стадия	Лист	Листов
П	18	103

выпуск 18.10.2026 № d119044df4 · стр. 18 из 103

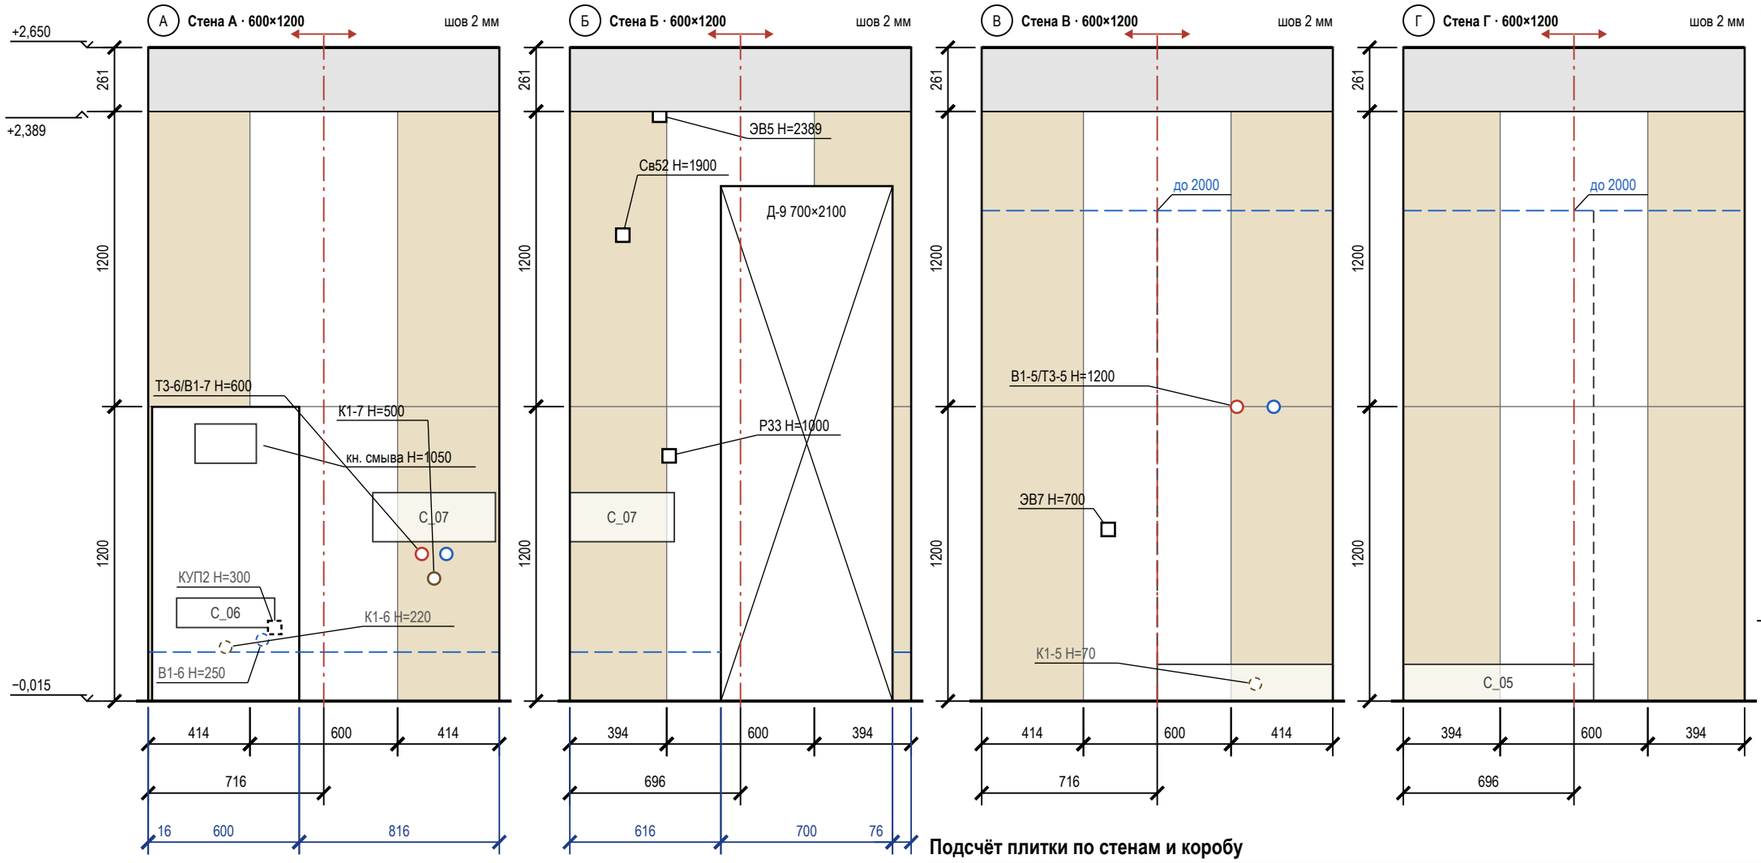

Условные обозначения

- плитка целая; тонкая линия — шов
- плитка с подрезкой (размер — на цепочке)
- ось старта; стрелки — направление укладки
- верх гидроизоляции: 200 от ЧП, в мокрой зоне — «до …»
- проём — не облицовывается
- сантехприбор: габарит, высота по практике
- граница душевой зоны (ограждение)
- короб инсталляции, в нём кнопка смыва 250×160
- вывод В1 (код — в ведомости привязок)
- вывод Т3 (код — в ведомости привязок)
- вывод К1 (код — в ведомости привязок)
- вывод за прибором / в коробе (не на сетке)
- электроточка: марка и Н — по листам ЭОМ
- отметка уровня, м: ±0,000 — чистый пол жилых помещений
- низ потолка; серая полоса — стена без плитки
- (А) обозначение стены А–Г (как на развёртках)

Подсчёт плитки по стенам и коробу

Поверхность	L × H, мм	S, м²	Целых	Подр.	С запасом	Подрезки: край / верх, мм
стена А	1432 × 2404	2,84	1	5	7	414 / 414; целый ряд
короб (ст. А)	600×1200×250	1,47	1	3	5	лицо 600; бок. 250
стена Б	1392 × 2404	1,99	0	6	7	394 / 394; целый ряд
стена В	1432 × 2404	3,56	2	4	7	414 / 414; целый ряд
стена Г	1392 × 2404	3,46	2	4	7	394 / 394; целый ряд
Итого		**13,32**	**6**	**22**	**33**	

Сдвиг точек под раскладку

Точка (ВК, ЭОМ)	Стена	Проект: от угла / Н	Под раскладку: от угла / Н	Сдвиг, мм
Т3-6/В1-7, К1-7	А	1166 / 600, 500	1017 / 600, 500	−149 на шов
Св52	Б	216 / 1900	94 / 1900	−122 в центр плитки
ЭВ5	Б	366 / 2389	395 / 2343	+29 на шов; Н −46
В1-5/Т3-5	В	1116 / 1200	1017 / 1141	−99 на шов; Н −59
ЭВ7	В	516 / 700	415 / 700	−101 на шов


Примечания

1. Вид изнутри, стены по часовой стрелке А → Г. Высоты — от чистого пола (−0,015), отметки — от ±0,000. Раскладка от чистовых размеров (штукатурка 10 + клей 5 + плитка 9 мм), подрезки чистые; старт — от оси стены, ряды от пола целыми.
2. Верх плитки +2,389, потолок +2,650, зазор 261 мм: потолок ГКЛ опустить до +2,392 (шов 3 мм, герметик) согласовать с монтажником ГКЛ; иначе профиль-окантовка, полосу окрасить в цвет потолка. Подрезной ряд 256 мм не делать.
3. Точки из таблицы сдвигов переносятся до черновой разводки: смеситель — по оси пары В1 + Т3; вывод на оси прибора — вместе с прибором, иначе старт раскладки — на ось прибора.
4. За приборами и в коробе (В1-6, К1-6, КУП2, К1-5) — штриховым кольцом.
5. Гидроизоляция: 200 мм от ЧП по периметру; у душа — до 2000 и 500 мм за поддон (СП 29.13330.2011, п. 7.2 — на высоту замачивания); углы — лентой; акт скрытых работ, пролив.
6. Короб 600×1200×250: лицо 600 мм от оси кнопки смыва, боковины, полка; углы — запил 45° или профиль; за коробом плитку не кладут.
7. Между коробом и углом полоса 16 мм — довести короб до угла.

					Проект: Квартира 103 м²
	Лист	№ док.	Подпись	Дата	Раскладка плитки. Ванная мастер. Развёртки стен
Дизайнер	Кырлан А.С.			18.10.26	

Стадия	Лист	Листов
П	19	103

выпуск 18.10.2026 № d119044df4 · стр. 19 из 103

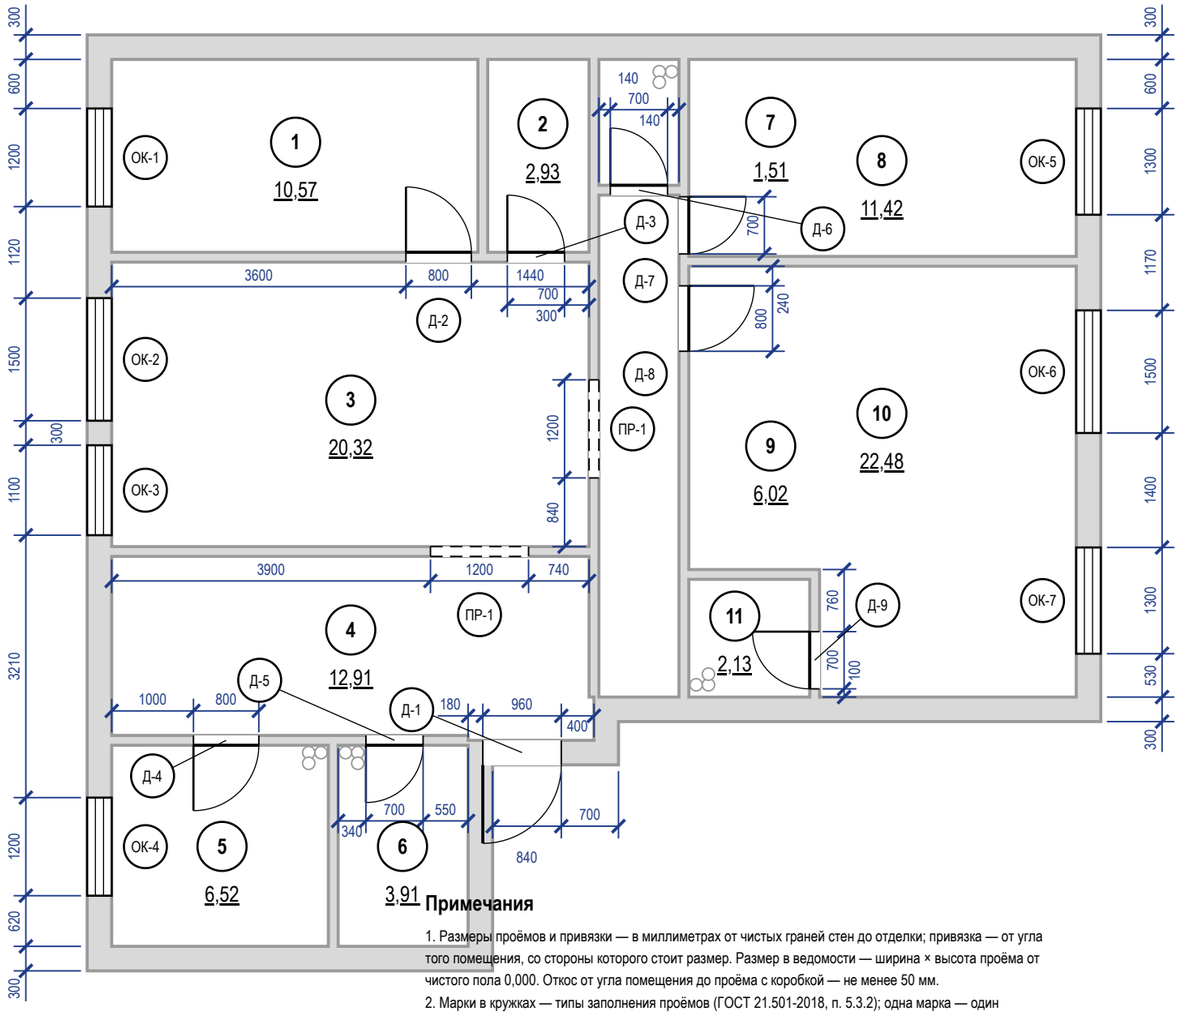

Ведомость заполнения проёмов

Марка	Наименование, обозначение	Проём ш×в, мм	Кол.	Откр.	Отделка полотна	Фурнитура	Прим.
Д-1	Блок дверной входной, ГОСТ 31173-2016	960×2100	1	Л	в комплекте блока	в комплекте блока (замки, глазок)	наружу
Д-2	Дверь скрытого монтажа, ТУ изготовителя	800×2100	1	П	окраска No. 291 с двух сторон	скрытые петли 3D, магнитный замок	
Д-3	Дверь скрытого монтажа, ТУ изготовителя	700×2100	1	П	S 0502-Y — пом. 2, No. 291 — пом. 3	скрытые петли 3D, магнитный замок	
Д-4	Дверь скрытого монтажа, ТУ изготовителя	800×2100	1	Л	окраска No. 291 с двух сторон	скрытые петли 3D, магнитный замок	
Д-5	Дверь скрытого монтажа, ТУ изготовителя	700×2100	1	Л	в тон облицовки — пом. 6, No. 291 — пом. 4	скрытые петли 3D, магнитный замок, фиксатор WC	порог 15
Д-6	Дверь скрытого монтажа, ТУ изготовителя	700×2100	1	П	S 0502-Y — пом. 7, No. 291 — пом. 9	скрытые петли 3D, магнитный замок	
Д-7	Дверь скрытого монтажа, ТУ изготовителя	700×2100	1	П	окраска No. 291 с двух сторон	скрытые петли 3D, магнитный замок	
Д-8	Дверь скрытого монтажа, ТУ изготовителя	800×2100	1	П	окраска No. 291 с двух сторон	скрытые петли 3D, магнитный замок	
Д-9	Дверь скрытого монтажа, ТУ изготовителя	700×2100	1	Л	в тон облицовки — пом. 11, No. 291 — пом. 10	скрытые петли 3D, магнитный замок, фиксатор WC	порог 15
ПР-1	Портал без заполнения	1200×2100	2				пом. 3; б/п
ОК-1	Блок оконный, ГОСТ 23166-2021; стекло — триплекс	1200×1560	1				низ 720
ОК-2	Блок оконный, ГОСТ 23166-2021; стекло — триплекс	1500×1550	1				низ 735
ОК-3	Блок оконный, ГОСТ 23166-2021; стекло — триплекс	1100×1550	1				низ 735
ОК-4	Блок оконный, ГОСТ 23166-2021; стекло — триплекс	1200×1550	1				низ 763
ОК-5	Блок оконный, ГОСТ 23166-2021; стекло — триплекс	1300×1552	1				низ 783
ОК-6	Блок оконный, ГОСТ 23166-2021; стекло — триплекс	1500×1548	1				низ 825
ОК-7	Блок оконный, ГОСТ 23166-2021; стекло — триплекс	1300×1548	1				низ 825


Примечания

1. Размеры проёмов и привязки — в миллиметрах от чистых граней стен до отделки; привязка — от угла того помещения, со стороны которого стоит размер. Размер в ведомости — ширина × высота проёма от чистого пола 0,000. Откос от угла помещения до проёма с коробкой — не менее 50 мм.
2. Марки в кружках — типы заполнения проёмов (ГОСТ 21.501-2018, п. 5.3.2); одна марка — один типоразмер; количество сверено с планом.
3. Открывание: Л — петли слева, П — справа, если смотреть со стороны, куда открывается полотно (на себя).
4. Остекление окон: ОК-1 (пом. 1) — триплекс; ОК-2 (пом. 3) — триплекс; ОК-3 (пом. 3) — триплекс; ОК-4 (пом. 5) — триплекс; ОК-5 (пом. 8) — триплекс; ОК-6 (пом. 10) — триплекс; ОК-7 (пом. 10) триплекс. Тип стекла указать при заказе оконных блоков; замена на другое стекло — только по согласованию с автором проекта.
5. ОК-1, ОК-2, ОК-3, ОК-4, ОК-5, ОК-6, ОК-7: низ остекления 720 и 735 и 763 и 783 и 825 мм — ниже 900 мм от чистого пола, поэтому окно заказывать с безопасным стеклом (триплекс); ограждение проёма в проекте не задано (СП 54.13330.2022, п. 6.4.9; ГОСТ Р 56926).
6. Скрытые двери (Д-2…Д-9): проём замерить в чистоте; блок заказать до штукатурки (≈ 30 дн.), короб ставить до штукатурки; полотно навесить после чистовой отделки, красить в цвет стен. Порядок практика монтажа, изготовитель подтверждает.
7. Д-2…Д-9 — существующие проёмы, до техзаключения не расширять.
8. Размеры проёмов и привязки сняты со скана плана заказчика и на объекте не замерены (обмерный план — лист 3).
9. Экспликация помещений — лист 3; в марках помещений — номер и площадь, м².
10. Привязка проёма к углу помещения меньше 1 мм на листе, размер на плане не показан: Д-7 — 30 мм.

					Проект: Квартира 103 м²
	Лист	№ док.	Подпись	Дата	
Дизайнер	Кырлан А.С.			18.10.26	План размещения дверей

Стадия	Лист	Листов
П	20	103

выпуск 18.10.2026 № d119044df4 · стр. 20 из 103

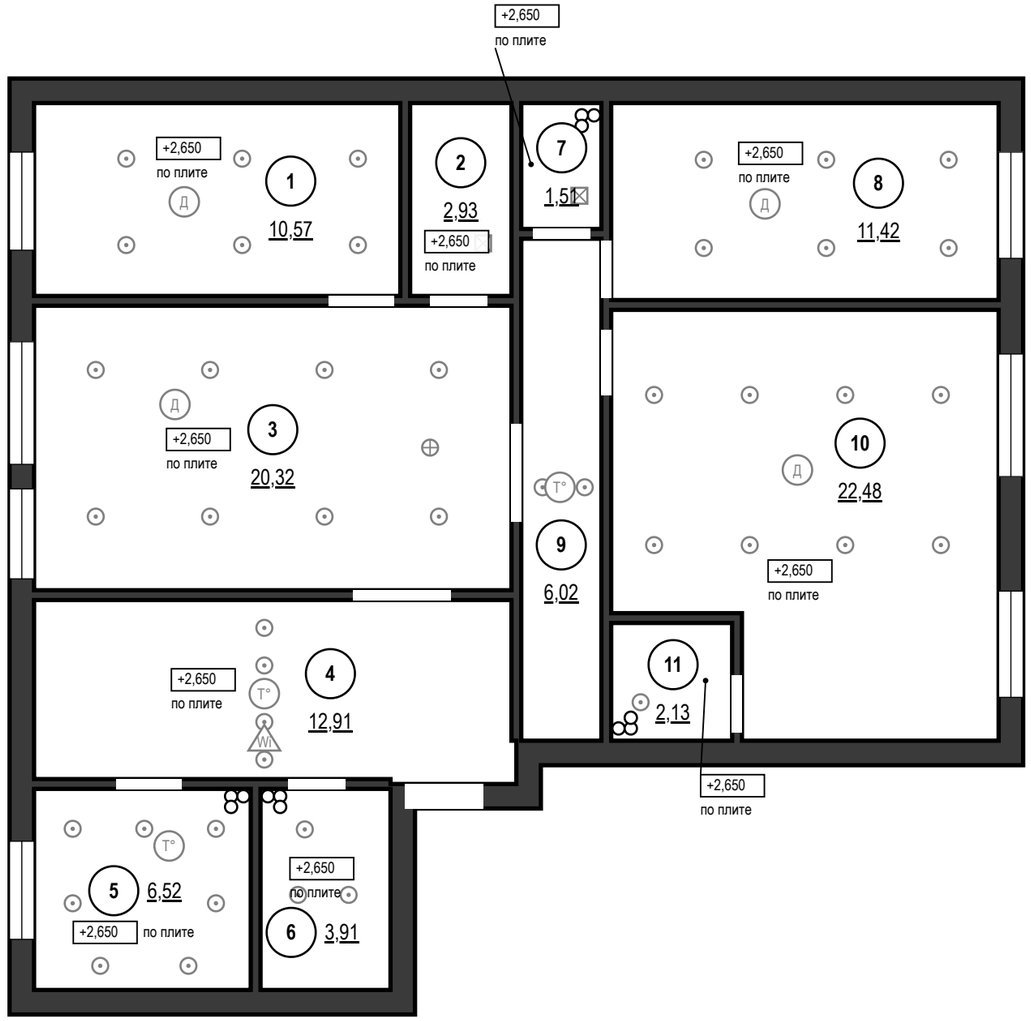

Ведомость потолков

Пом.	Марка	Конструкция	Низ	S, м²	Q
1		по плите, окраска	+2,650	10,57	
2		по плите, окраска	+2,650	2,93	
3		по плите, окраска	+2,650	20,32	
4		по плите, окраска	+2,650	12,91	
5		по плите, окраска	+2,650	6,52	
6		по плите, окраска	+2,650	3,91	
7		по плите, окраска	+2,650	1,51	
8		по плите, окраска	+2,650	11,42	
9		по плите, окраска	+2,650	6,02	
10		по плите, окраска	+2,650	22,48	
11		по плите, окраска	+2,650	2,13	
		Итого		**100,72**	

Ведомость вырезов и закладных в потолке

Марка	Устройство	Кол.	Пом.
	Светильник встраиваемый (марки — план освещения)	46	1, 3, 4, 5, 6, 8, 9, 10, 11
	Светильник накладной (марки — план освещения)	2	2, 7
	Светильник подвесной (марки — план освещения)	1	3
ИП2, ИП1, ИП2, ИП1	Извещатель дымовой	4	1, 3, 8, 10
ИП3, ИП4, ИП6	Извещатель тепловой	3	4, 5, 9
AP1	Точка доступа Wi-Fi, PoE	1	4


Примечания

1. За отметку ±0,000 принят уровень чистого пола сухих помещений (готовое покрытие), а не существующего пола; пол пом. 6, 11 — −0,015; существующий пол снимается до плиты, его отметка не замерена. Отметки в прямоугольниках — низ потолка; низ плиты перекрытия +2,650. Марка потолка — одна конструкция и отметка на весь альбом.
2. Светильники и потолочные устройства — подложка с планов освещения, слаботочных систем и вентиляции (положение — по ним); вырезы и закладные — по ведомости на листе, до обшивки; отверстия не совмещать с профилями.
3. Пом. 1, 2, 3, 4, 5, 6, 7, 8, 9, 10, 11 — потолок по плите без подвесной системы; отделка — по ведомости отделки.

					Проект: Квартира 103 м²
	Лист	№ док.	Подпись	Дата	План потолков
Дизайнер	Кырлан А.С.			18.10.26	

Стадия	Лист	Листов
П	21	103

выпуск 18.10.2026 № d119044df4 · стр. 21 из 103

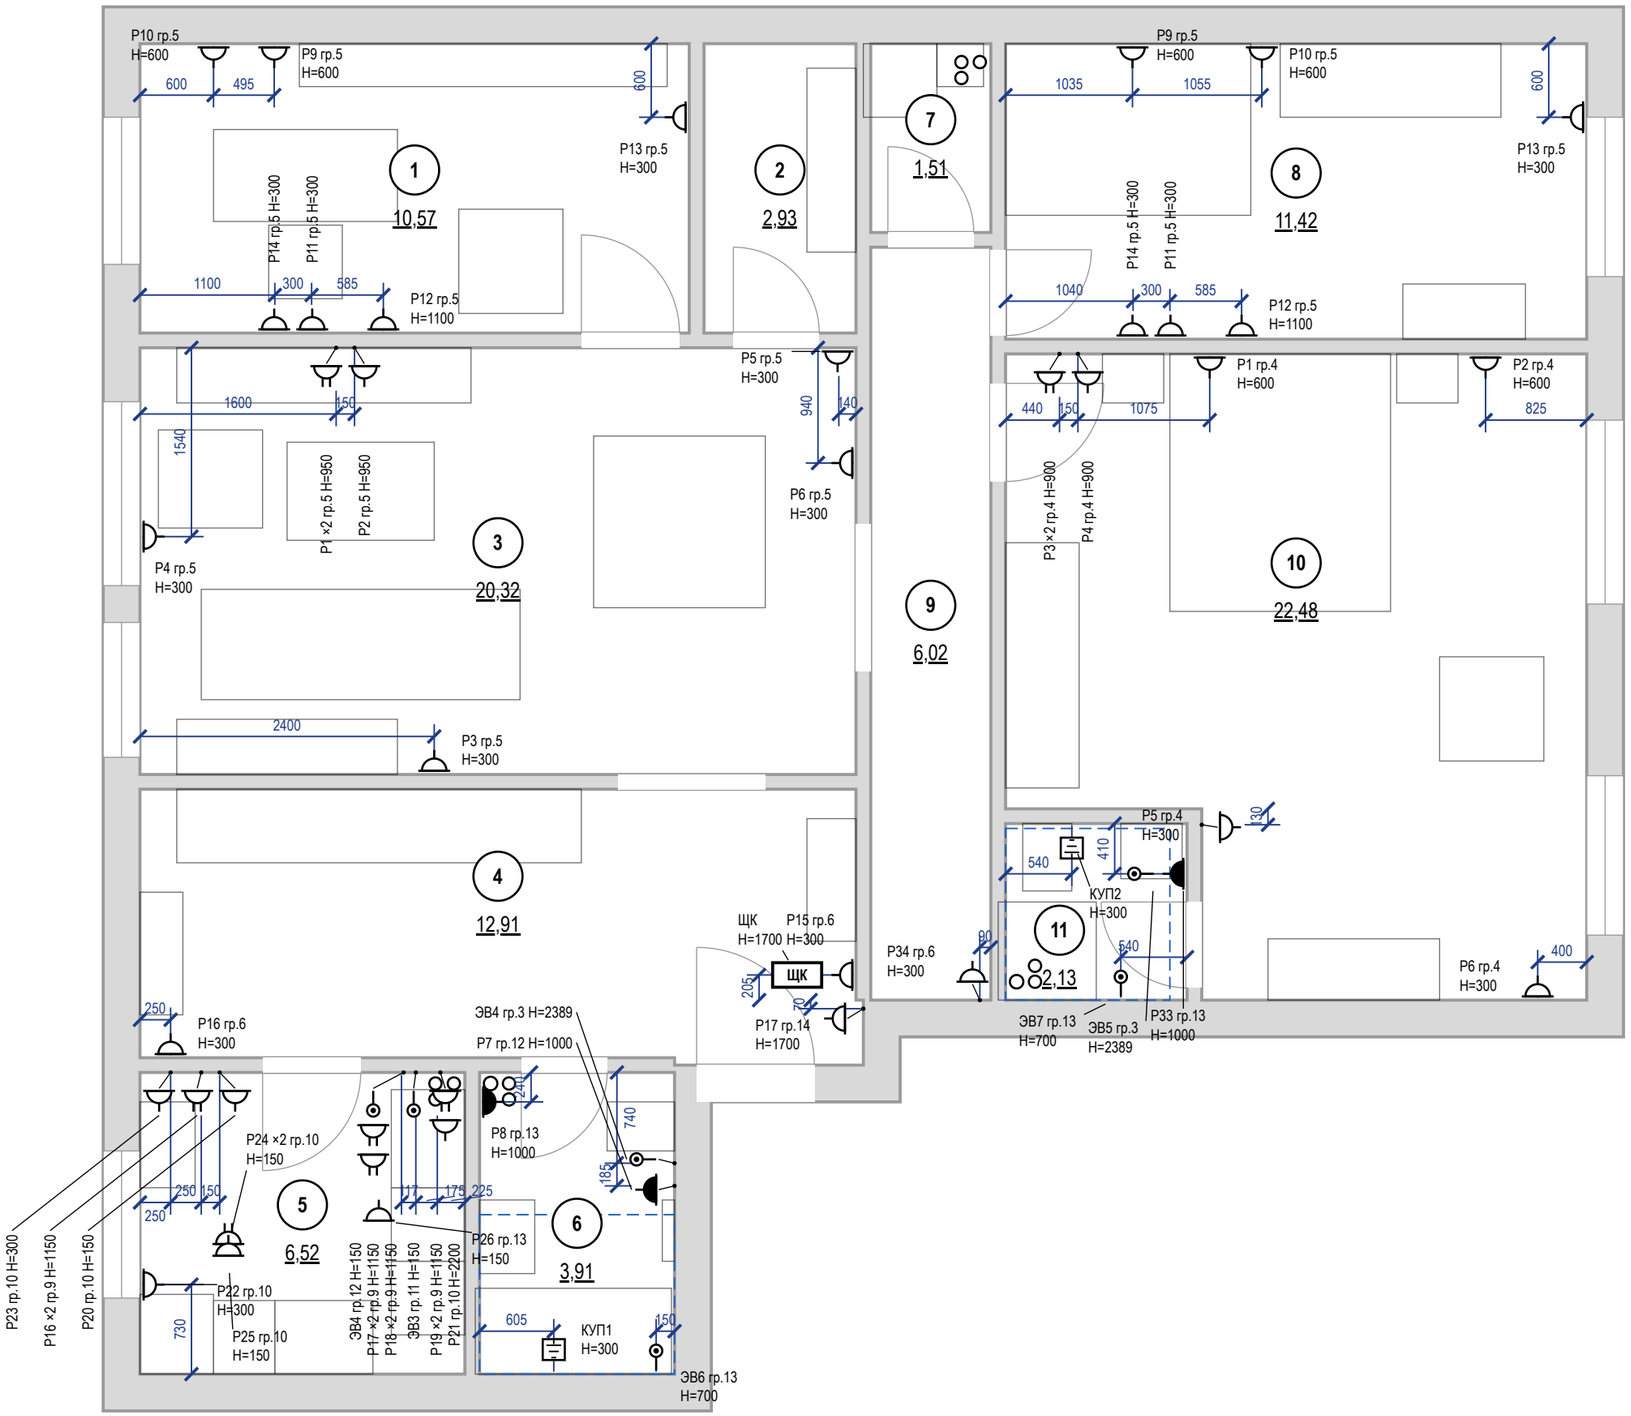

Условные обозначения


- розетка с заземляющим контактом; у знака — марка, ×N постов в рамке, гр. — группа щита, H — высота оси, мм
- то же, рамка на 2 поста (число черточек — число постов)
- розетка влагозащищённая IP44
- вывод кабеля для подключения прибора (без розетки), марка ЭВ
- КУП — коробка уравнивания потенциалов (ДСУП), проводник к шине PE щита
- ЩК — щит квартирный
- знак разведён для читаемости: точка на стене — у выноски, привязка — до неё
- граница зоны 2 ванной (600 мм от ванны/поддона)
- мебель и сантехприборы — подложка
- стояк: К1 — канализация, В1 — ХВС, Т3 — ГВС
- 1 — номер помещения, площадь м²

Примечания

1. За отметку 0,000 принят уровень чистого пола. Высоты H — от чистого пола до оси изделия; привязки — от чистовой грани стены до оси механизма (у рамки на несколько постов — до оси рамки).
2. Высота установки, не указанная на плане: розетки — 300 мм от чистого пола; выводы кабеля — по паспорту прибора.
3. Розетки в санузле — только вне зон 0–2 (ПУЭ 7.1.48, ГОСТ Р 50571.7.701-2024), IP44, через УЗО 30 мА.
4. Розеточные и мокрые линии — через УЗО или дифавтомат с током утечки не более 30 мА (ПУЭ 7.1.79); в санузле выполнить ДСУП (ПУЭ 7.1.87–7.1.88).
5. Кабель — медный, исполнение нг(A)-LS (ГОСТ 31565-2012); скрытая прокладка только горизонтально и вертикально, фактические трассы зафиксировать исполнительной схемой до закрытия отделкой.
6. Расчёт нагрузок, токов КЗ, селективности и сечений — по проекту ЭОМ организации с допуском СРО; лист задаёт состав, расположение и группы.
7. Выводы кухонной техники — после утверждения проекта кухни (ориентировочно); привязки выводов даны от осей модулей гарнитура и пересматриваются вместе с проектом кухни.
8. Электрический тёплый пол проектом не предусмотрен; при решении заказчика устроить — отдельный лист «План тёплых полов»: контуры с отступом 100 мм от стен и мебели без ножек, датчик в гофре, терморегулятор, своя группа щита через УЗО 30 мА.
9. Ведомости электроточек, изделий, светильников и расшифровка клавиш — лист «Ведомость электроточек и изделий».

					Проект: Квартира 103 м²
	Лист	№ док.	Подпись	Дата	План розеток и электровыводов
Дизайнер	Кырлан А.С.			18.10.26	Стадия: П; Лист: 22; Листов: 103

выпуск 18.10.2026 № d119044df4 · стр. 22 из 103

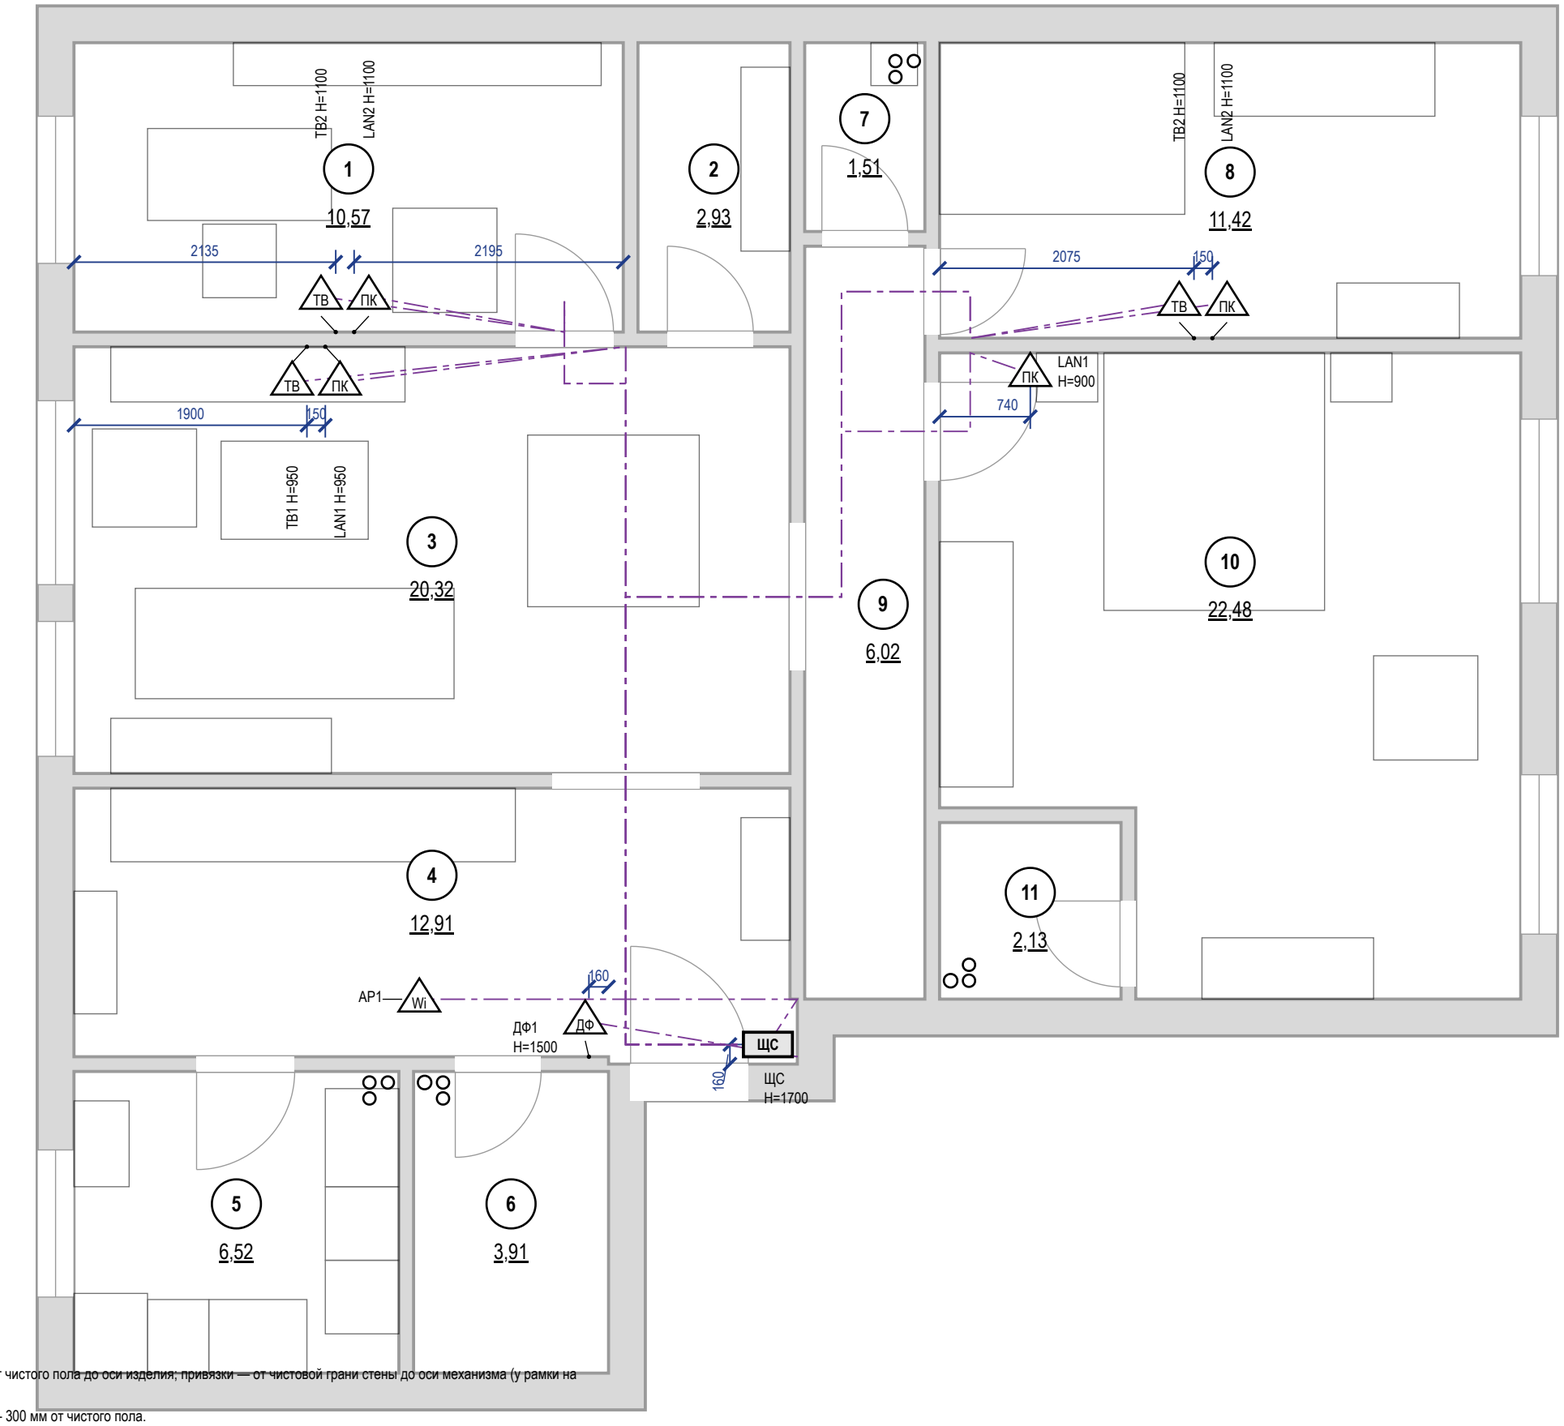


Примечания

1. За отметку 0,000 принят уровень чистого пола. Высоты Н — от чистого пола до оси изделия; привязки — от чистовой грани стены до оси механизма (у рамки на несколько постов — до оси рамки).
2. Высота установки, не указанная на плане: розетки LAN и ТВ — 300 мм от чистого пола.
3. Слаботочные кабели — отдельно от силовых: в своей трубе или лотке, при параллельной прокладке не ближе 100 мм к силовым, пересечения под прямым углом; каждую точку — отдельным кабелем от ЩС без скруток.
4. Трассы на листе — принципиальные; фактические зафиксировать исполнительной схемой до закрытия отделкой. Силовые линии, УЗО 30 мА, ДСУП, кабель нг(А)-LS — по листам розеток и щита.
5. Проект силовой части и расчёт токов КЗ — по проекту ЭОМ; слаботочная часть согласуется с провайдером и управляющей компанией (домофон, коллективное ТВ).

					Проект: Квартира 103 м²
	Лист	№ док.	Подпись	Дата	
Дизайнер	Кырлан А.С.			18.10.26	План слаботочных сетей

Стадия	Лист	Листов
П	23	103

выпуск 18.10.2026 № d119044df4 · стр. 23 из 103

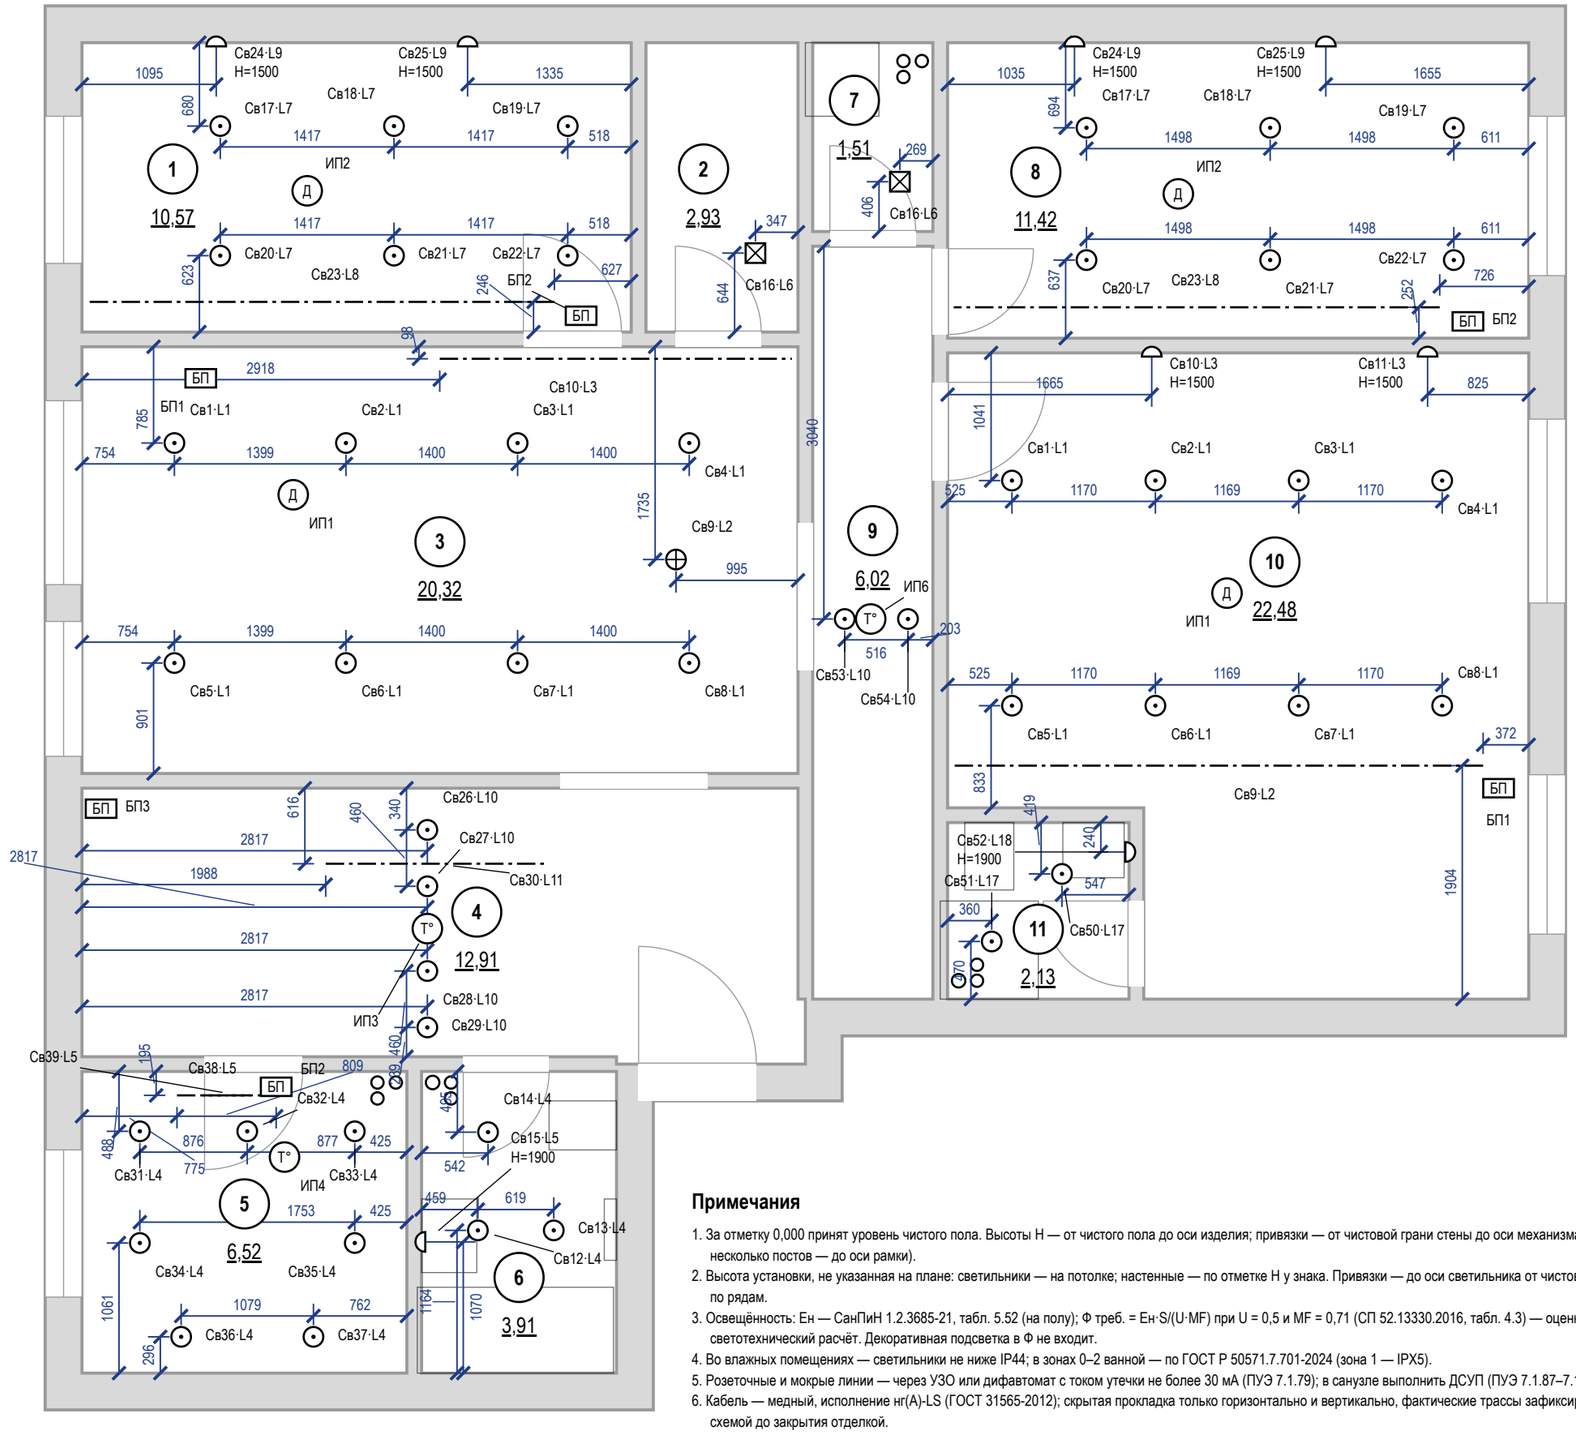

Примечания

1. За отметку 0,000 принят уровень чистого пола. Высоты Н — от чистого пола до оси изделия; привязки — от чистовой грани стены до оси механизма (у рамки на несколько постов — до оси рамки).
2. Высота установки, не указанная на плане: светильники — на потолке; настенные — по отметке Н у знака. Привязки — до оси светильника от чистовой грани стены, по рядам.
3. Освещённость: Ен — СанПиН 1.2.3685-21, табл. 5.52 (на полу); Ф треб. = Ен·S/(U·MF) при U = 0,5 и MF = 0,71 (СП 52.13330.2016, табл. 4.3) — оценка, не светотехнический расчёт. Декоративная подсветка в Ф не входит.
4. Во влажных помещениях — светильники не ниже IP44; в зонах 0–2 ванной — по ГОСТ Р 50571.7.701-2024 (зона 1 — IPX5).
5. Розеточные и мокрые линии — через УЗО или дифавтомат с током утечки не более 30 мА (ПУЭ 7.1.79); в санузле выполнить ДСУП (ПУЭ 7.1.87–7.1.88).
6. Кабель — медный, исполнение нг(A)-LS (ГОСТ 31565-2012); скрытая прокладка только горизонтально и вертикально, фактические трассы зафиксировать исполнительной схемой до закрытия отделкой.
7. Расчёт нагрузок, токов КЗ, селективности и сечений — по проекту ЭОМ организации с допуском СРО; лист задаёт состав, расположение и группы.
8. Ведомость светильников — лист «Ведомость электроточек и изделий».

					Проект: Квартира 103 м²
	Лист	№ док.	Подпись	Дата	
Дизайнер	Кырлан А.С.			18.10.26	План освещения

Стадия	Лист	Листов
П	24	103

выпуск 18.10.2026 № d119044df4 · стр. 24 из 103

Спецификация светильников

Поз.	Марки	Наименование	Установка	Кол.	P, Вт	Σ P, Вт	Ф, лм	Тц, К	Ra	Угол, °	IP	Дим.	Группа	Пом.
1	Св17–Св22	Встраиваемый точечный	встраиваемый	12	12	144	1050	2700	90	—	20	—	L7	1, 8
2	Св23	Лента светодиодная 24 В	в коробе, профиль с рассеивателем	24,6 м	9,6/м	236,2	900/м	2700	90	—	20	да	L8	1, 8
3	Св10, Св11, Св24, Св25	Настенный (бра)	на стене, H=1500	6	6	36	400	2700	90	60	20	да	L3, L9	1, 8, 10
4	Св16	Потолочный накладной	на потолке, засветка стены	2	10	20	900	3000	90	—	20	—	L6	2, 7
5	Св1–Св8, Св31–Св37	Встраиваемый точечный	встраиваемый	15	12	180	1000	3000	90	—	20	—	L1, L4	3, 5
6	Св9	Подвесной	подвес, низ H=1600	1	15	15	1200	2700	90	—	20	—	L2	3
7	Св10	Лента светодиодная 24 В	в коробе, профиль с рассеивателем	5 м	9,6/м	48	900/м	2700	90	—	20	да	L3	3
8	Св26–Св29, Св53, Св54	Встраиваемый точечный	встраиваемый	6	7	42	600	3000	90	—	20	—	L10	4, 9
9	Св30	Лента светодиодная 24 В	в коробе, профиль с рассеивателем, датчик движения	1,8 м	4,8/м	8,6	150/м	2700	90	—	20	нет	L11	4
10	Св38, Св39	Линейный светильник	на поверхности	1,2 м	8	16	700	3000	90	—	20	—	L5	5
11	Св12–Св14, Св51	Встраиваемый точечный	встраиваемый	4	6	24	500	3000	90	—	44	—	L4, L17	6, 11
12	Св15, Св52	Настенный светильник над зеркалом, драйвер встроен	над зеркалом, H=1900	2	8	16	600	3000	90	—	44	—	L5, L18	6, 11
13	Св1–Св8	Встраиваемый точечный	встраиваемый	8	12	96	1000	2700	90	—	20	—	L1	10
14	Св9	Лента светодиодная 24 В	в коробе, профиль с рассеивателем	15,5 м	9,6/м	148,8	900/м	2700	90	—	20	да	L2	10
15	Св50	Встраиваемый точечный	встраиваемый	1	7	7	600	3000	90	—	44	—	L17	11
		Итого		**57 шт + 48,1 м**		**1037,6**								

Слои света по помещениям

Пом.	Помещение	Слои света и группы включения (марки светильников)	Тц, К	Ra	Σ P, Вт	Сцен.
1	Кабинет-библиотека	общий — L7 (Св17–Св22); рабочий — L9 (Св24, Св25); акцентный — L8 (Св23)	2700	90	202,1	1
2	Кладовая	общий — L6 (Св16)	3000	90	10	—
3	Гостиная-столовая	общий — L1 (Св1–Св8); рабочий — L2 (Св9); акцентный — L3 (Св10)	2700 / 3000	90	159	4
4	Прихожая-холл	общий — L10 (Св26–Св29); ночной — L11 (Св30)	2700 / 3000	90	36,6	—
5	Кухня	общий — L4 (Св31–Св37); рабочий — L5 (Св38, Св39)	3000	90	100	—
6	Ванная	общий — L4 (Св12–Св14); рабочий — L5 (Св15)	3000	90	26	—
7	Постирочная	общий — L6 (Св16)	3000	90	10	—
8	Спальня 2	общий — L7 (Св17–Св22); рабочий — L9 (Св24, Св25); акцентный — L8 (Св23)	2700	90	202,1	1
9	Коридор	общий — L10 (Св53, Св54)	3000	90	14	—
10	Спальня мастер	общий — L1 (Св1–Св8); рабочий — L3 (Св10, Св11); акцентный — L2 (Св9)	2700	90	256,8	2
11	Ванная мастер	общий — L17 (Св50, Св51); рабочий — L18 (Св52)	3000	90	21	—

LED-ленты, линейные светильники и блоки питания

Марка	Пом.	L, м	U, В	Вт/м	Σ P, Вт	БП	P БП, Вт	Загр., %	Питание	Доступ к БП
Св23	1	12,3	24	9,6	118,1	БП2	200	126	с двух концов	люк 300×300 в коробе У1 у окна
Св10	3	5	24	9,6	48	БП1	200	98	с одного конца	люк 300×300 в коробе У1 у входа
Св30	4	1,8	24	4,8	8,6	БП3	20	43	с одного конца	в шкафу М16, верхняя полка
Св38	5	0,6	24	—	8	БП2	200	126	встроенный ввод	люк 300×300 в коробе У1 у окна
Св39	5	0,6	24	—	8	БП2	200	126	встроенный ввод	люк 300×300 в коробе У1 у окна
Св23	8	12,3	24	9,6	118,1	БП2	200	126	с двух концов	люк 300×300 в коробе У1 у окна
Св9	10	15,5	24	9,6	148,8	БП1	200	98	с двух концов	люк 300×300 в коробе У1 у входа

Сценарии освещения

Пом.	Сценарий	Группы и уровни, %	Чем включается
1	Вечер	L7 споты — 0; L8 подсветка короба — 100; L9 бра — 100	S4, S5, S6
3	Вечер	L1 общий свет (споты) — 0; L2 подвес над обеденным столом — 100; L3 лента в карнизе (диммер) — 50	S1, S2, S2 светорегулятор, S3
3	Гости	L1 общий свет (споты) — 100; L2 подвес над обеденным столом — 100; L3 лента в карнизе (диммер) — 100	S1, S2, S2 светорегулятор, S3
3	Кино	L1 общий свет (споты) — 0; L2 подвес над обеденным столом — 0; L3 лента в карнизе (диммер) — 20	S2, S2 светорегулятор, S3
3	Уборка	L1 общий свет (споты) — 100; L2 подвес над обеденным столом — 100; L3 лента в карнизе (диммер) — 0	S1, S2, S3
8	Вечер	L7 споты — 0; L8 подсветка короба — 100; L9 бра — 100	S4, S5, S6
10	Вечер	L1 общий свет (споты) — 0; L2 подвес над обеденным столом — 100; L3 лента в карнизе (диммер) — 100	S1, S2, S2 светорегулятор, S3
10	Уборка	L1 общий свет (споты) — 100; L2 подвес над обеденным столом — 100; L3 лента в карнизе (диммер) — 0	S1, S2, S3

Слои света

общий — равномерный свет помещения, по норме освещённости

рабочий — местный свет задачи: столешница, зеркало, чтение у кровати

акцентный — подсветка потолка, стен и ниш; не входит в поток общего света


ночной — путь спальня → санузел: не выше 2700 K, малая яркость, датчик движения

Примечания

1. Позиции и марки Св — те же, что на плане освещения (лист 24) и в ведомости светильников (лист «Ведомость электроточек и изделий»); группы L — по плану выключателей (лист 26).
2. Модели светильников не назначены: подбор по графам спецификации — поток, Тц, Ra, угол, IP и диммирование не хуже указанных, мощность не больше. IP 20 — сухие помещения.
3. Длина LED-ленты в карнизе — по линии карниза плана потолков (лист 21); Σ P = Вт/м × длина. Блок питания загружен не больше чем на 80 %; лента 24 В длиннее 10 м питается с двух концов; доступ к блоку питания — люк ревизии 300×300 мм или место, указанное в таблице.
4. Сценарии: уровень — доля максимальной яркости группы, %; 0 — группа выключена. Уровень ниже 100 % — только у групп на светорегуляторе (задний фронт, TE) с диммируемыми драйверами и блоками питания.
5. Мощность и поток — по паспортам принятых изделий, Σ P — установленная мощность освещения. Оценка освещённости — на плане освещения; это не светотехнический расчёт.

					Проект: Квартира 103 м²
	Лист	№ док.	Подпись	Дата	Спецификация светильников и сценарии освещения
Дизайнер	Кырлан А.С.			18.10.26	

Стадия	Лист	Листов
П	25	103

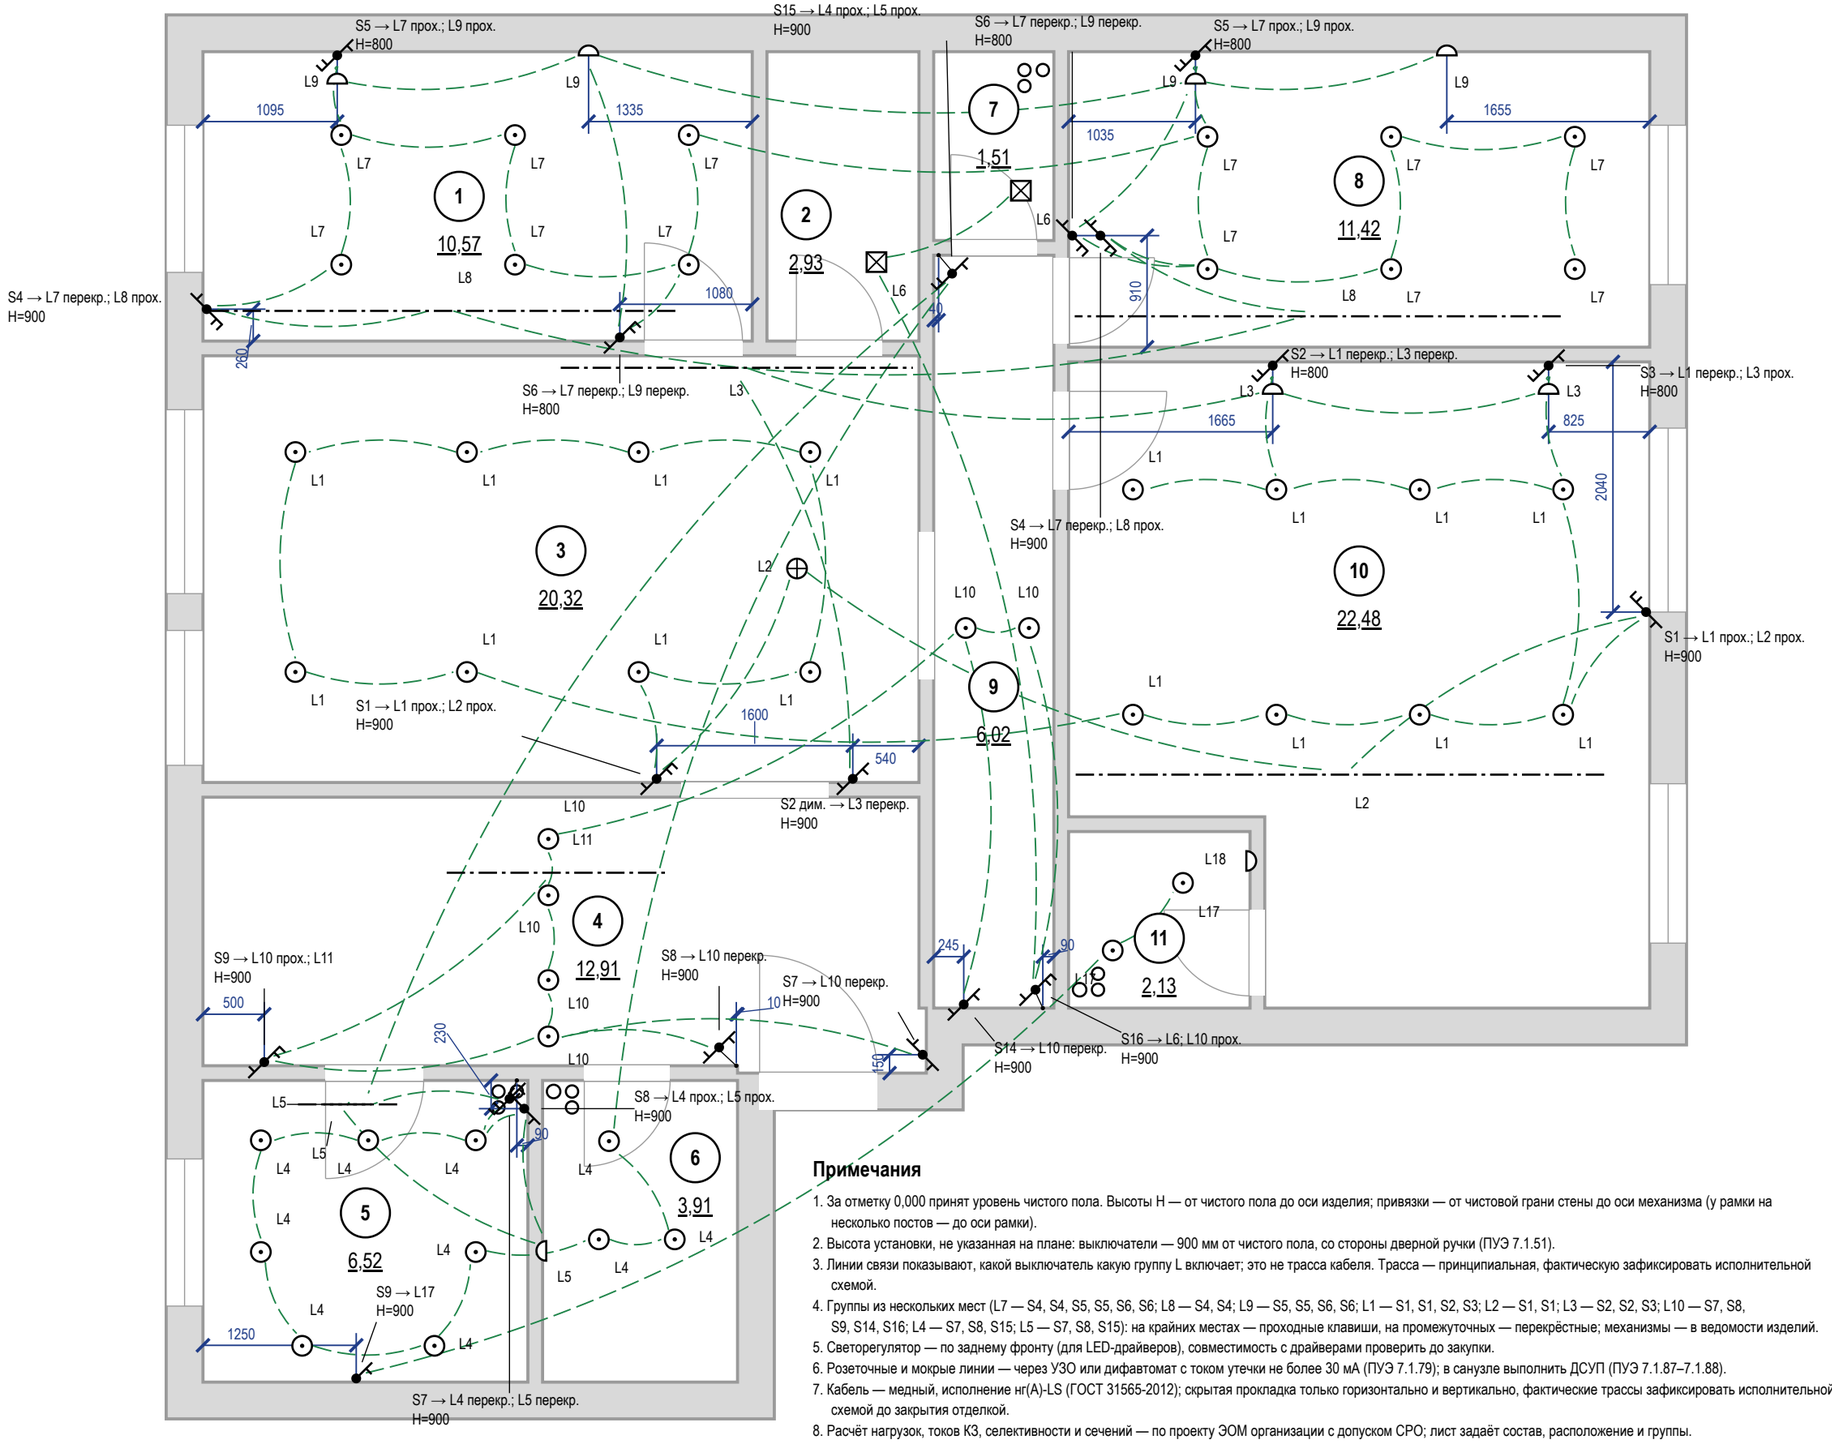


Примечания

1. За отметку 0,000 принят уровень чистого пола. Высоты H — от чистого пола до оси изделия; привязки — от чистовой грани стены до оси механизма (у рамки на несколько постов — до оси рамки).
2. Высота установки, не указанная на плане: выключатели — 900 мм от чистого пола, со стороны дверной ручки (ПУЭ 7.1.51).
3. Линии связи показывают, какой выключатель какую группу L включает; это не трасса кабеля. Трасса — принципиальная, фактическую зафиксировать исполнительной схемой.
4. Группы из нескольких мест (L7 — S4, S4, S5, S5, S6, S6; L8 — S4, S4; L9 — S5, S5, S6, S6; L1 — S1, S1, S2, S3; L2 — S1, S1; L3 — S2, S2, S3; L10 — S7, S8, S9, S14, S16; L4 — S7, S8, S15; L5 — S7, S8, S15): на крайних местах — проходные клавиши, на промежуточных — перекрёстные; механизмы — в ведомости изделий.
5. Светорегулятор — по заднему фронту (для LED-драйверов), совместимость с драйверами проверить до закупки.
6. Розеточные и мокрые линии — через УЗО или дифавтомат с током утечки не более 30 мА (ПУЭ 7.1.79); в санузле выполнить ДСУП (ПУЭ 7.1.87–7.1.88).
7. Кабель — медный, исполнение нг(A)-LS (ГОСТ 31565-2012); скрытая прокладка только горизонтально и вертикально, фактические трассы зафиксировать исполнительной схемой до закрытия отделкой.
8. Расчёт нагрузок, токов КЗ, селективности и сечений — по проекту ЭОМ организации с допуском СРО; лист задаёт состав, расположение и группы.
9. Группы без выключателя: L18 — назначить управление до монтажа.
10. Расшифровка клавиш и ведомость изделий — лист «Ведомость электроточек и изделий».

					Проект: Квартира 103 м²
	Лист	№ док.	Подпись	Дата	Управление светильниками
Дизайнер	Кырлан А.С.			18.10.26	

Стадия	Лист	Листов
П	26	103

выпуск 18.10.2026 № d119044df4 · стр. 26 из 103

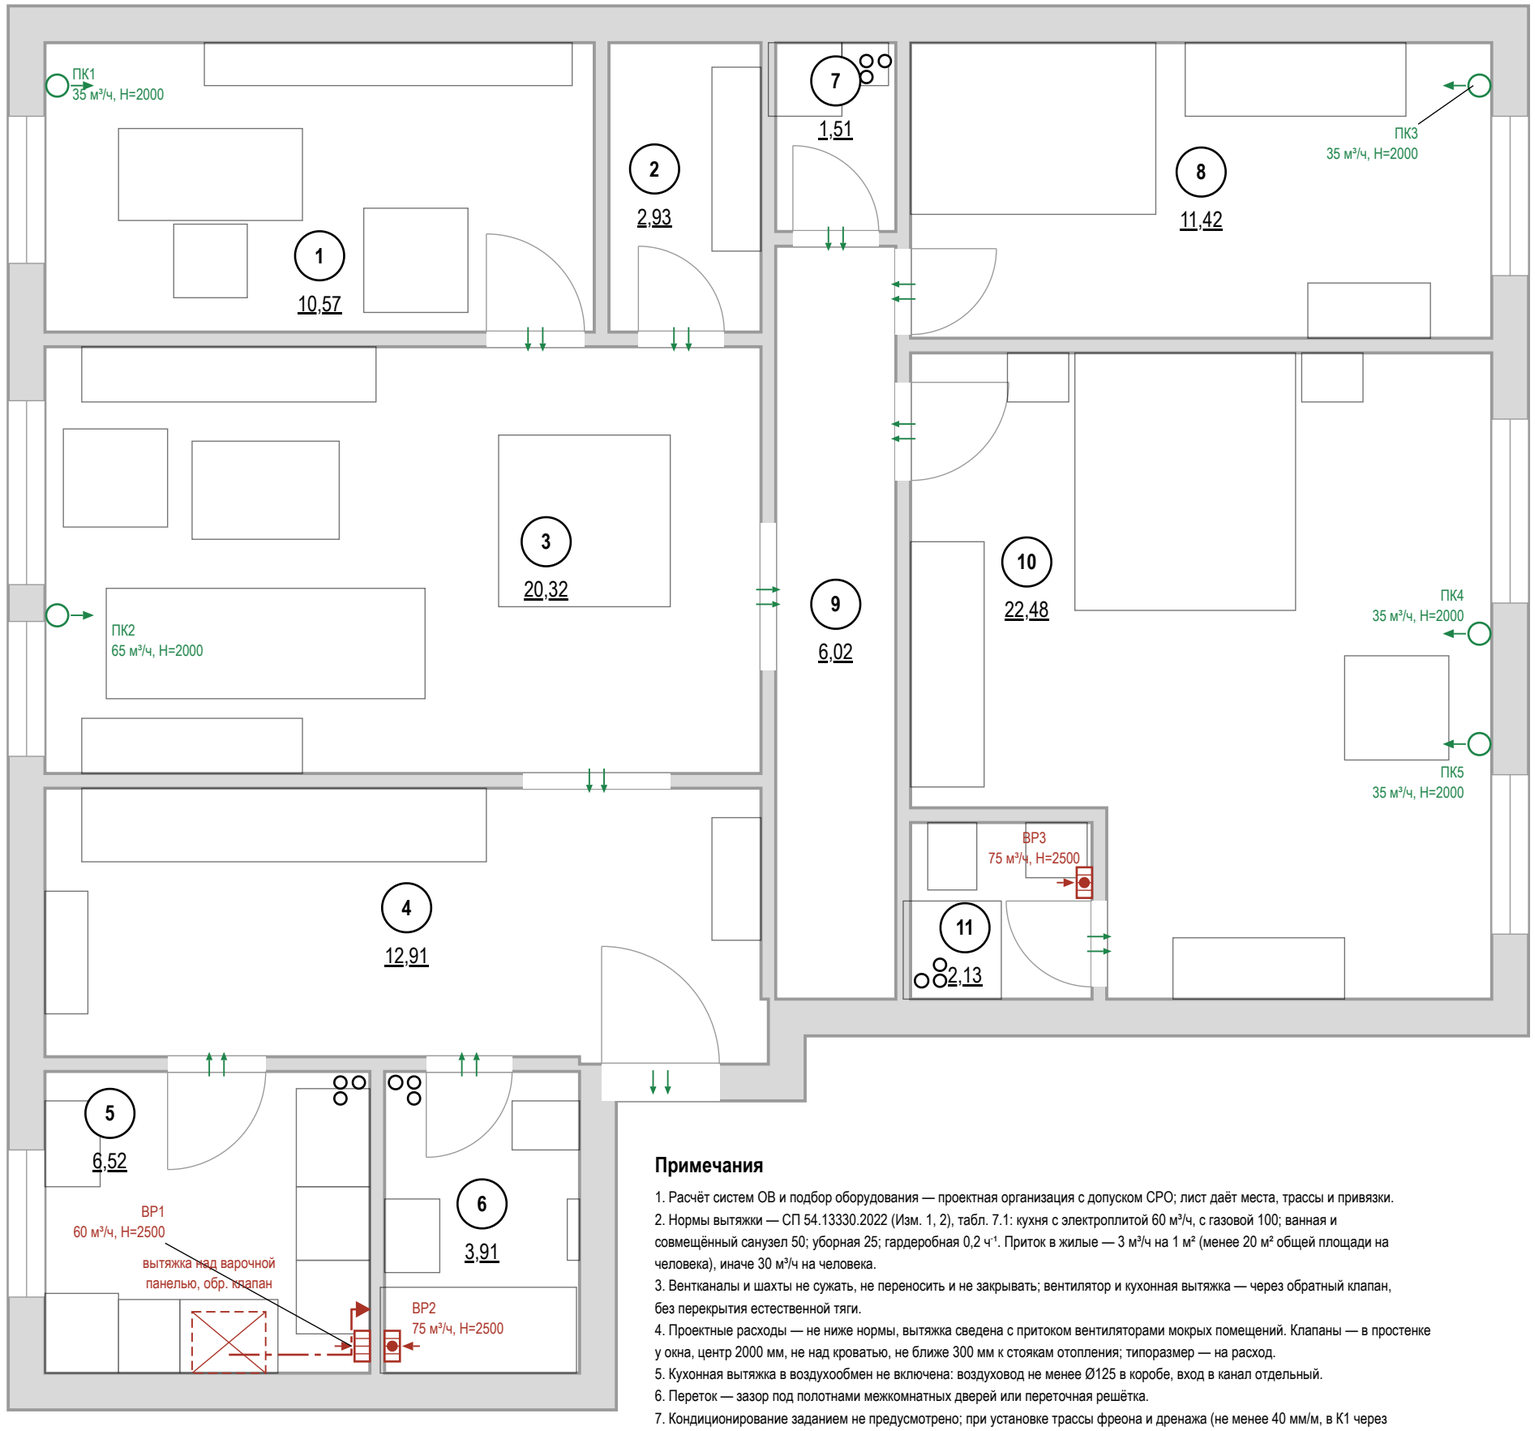

Условные обозначения

- стояк: К1 — канализация, В1 — ХВС, Т3 — ГВС
- номер помещения, площадь м²
- вытяжная решётка в вентканал: марка, расход м³/ч, Н центра от чистого пола
- вытяжная решётка с бытовым вентилятором и обратным клапаном: марка, расход, Н
- приточный клапан (КИВ) в наружной стене: марка, расход, Н центра
- переток: зазор под полотном или переточная решётка
- кухонная вытяжка над варочной панелью
- воздуховод кухонной вытяжки в коробе под потолком
- отдельный вход воздуховода в вентканал, обратный клапан

Воздухообмен, м³/ч

№	Помещение	Выт. норма	Выт. проект	Прит. норма	Прит. проект	Устрой ства
1	Кабинет-библиотека			32	35	ПК1
2	Кладовая	2				переток
3	Гостиная-столовая			61	65	ПК2
5	Кухня	60	60			ВР1
6	Ванная	50	75			ВР2
7	Постирочная	1				переток
8	Спальня 2			35	35	ПК3
10	Спальня мастер			68	70	ПК4, ПК5
11	Ванная мастер	50	75			ВР3
	Итого	**163**	**210**	**60**	**205**	

Воздухообмен квартиры — по большей из сумм притока и вытяжки: норма 163 м³/ч, проект 210 м³/ч.
Вытяжка не меньше притока — баланс сведён.


Примечания

1. Расчёт систем ОВ и подбор оборудования — проектная организация с допуском СРО; лист даёт места, трассы и привязки.
2. Нормы вытяжки — СП 54.13330.2022 (Изм. 1, 2), табл. 7.1: кухня с электроплитой 60 м³/ч, с газовой 100; ванная и совмещённый санузел 50; уборная 25; гардеробная 0,2 ч⁻¹. Приток в жилые — 3 м³/ч на 1 м² (менее 20 м² общей площади на человека), иначе 30 м³/ч на человека.
3. Вентканалы и шахты не сужать, не переносить и не закрывать; вентилятор и кухонная вытяжка — через обратный клапан, без перекрытия естественной тяги.
4. Проектные расходы — не ниже нормы, вытяжка сведена с притоком вентиляторами мокрых помещений. Клапаны — в простенке у окна, центр 2000 мм, не над кроватью, не ближе 300 мм к стоякам отопления; типоразмер — на расход.
5. Кухонная вытяжка в воздухообмен не включена: воздуховод не менее Ø125 в коробе, вход в канал отдельный.
6. Переток — зазор под полотнами межкомнатных дверей или переточная решётка.
7. Кондиционирование заданием не предусмотрено; при установке трассы фреона и дренажа (не менее 40 мм/м, в К1 через сифон) и питание заложить до черновых работ.
8. Привязки оборудования — по паспортам приобретённых моделей, до черновых работ.

					Проект: Квартира 103 м²
	Лист	№ док.	Подпись	Дата	План вентиляции
Дизайнер	Кырлан А.С.			18.10.26	

Стадия	Лист	Листов
П	27	103

выпуск 18.10.2026 № d119044df4 · стр. 27 из 103

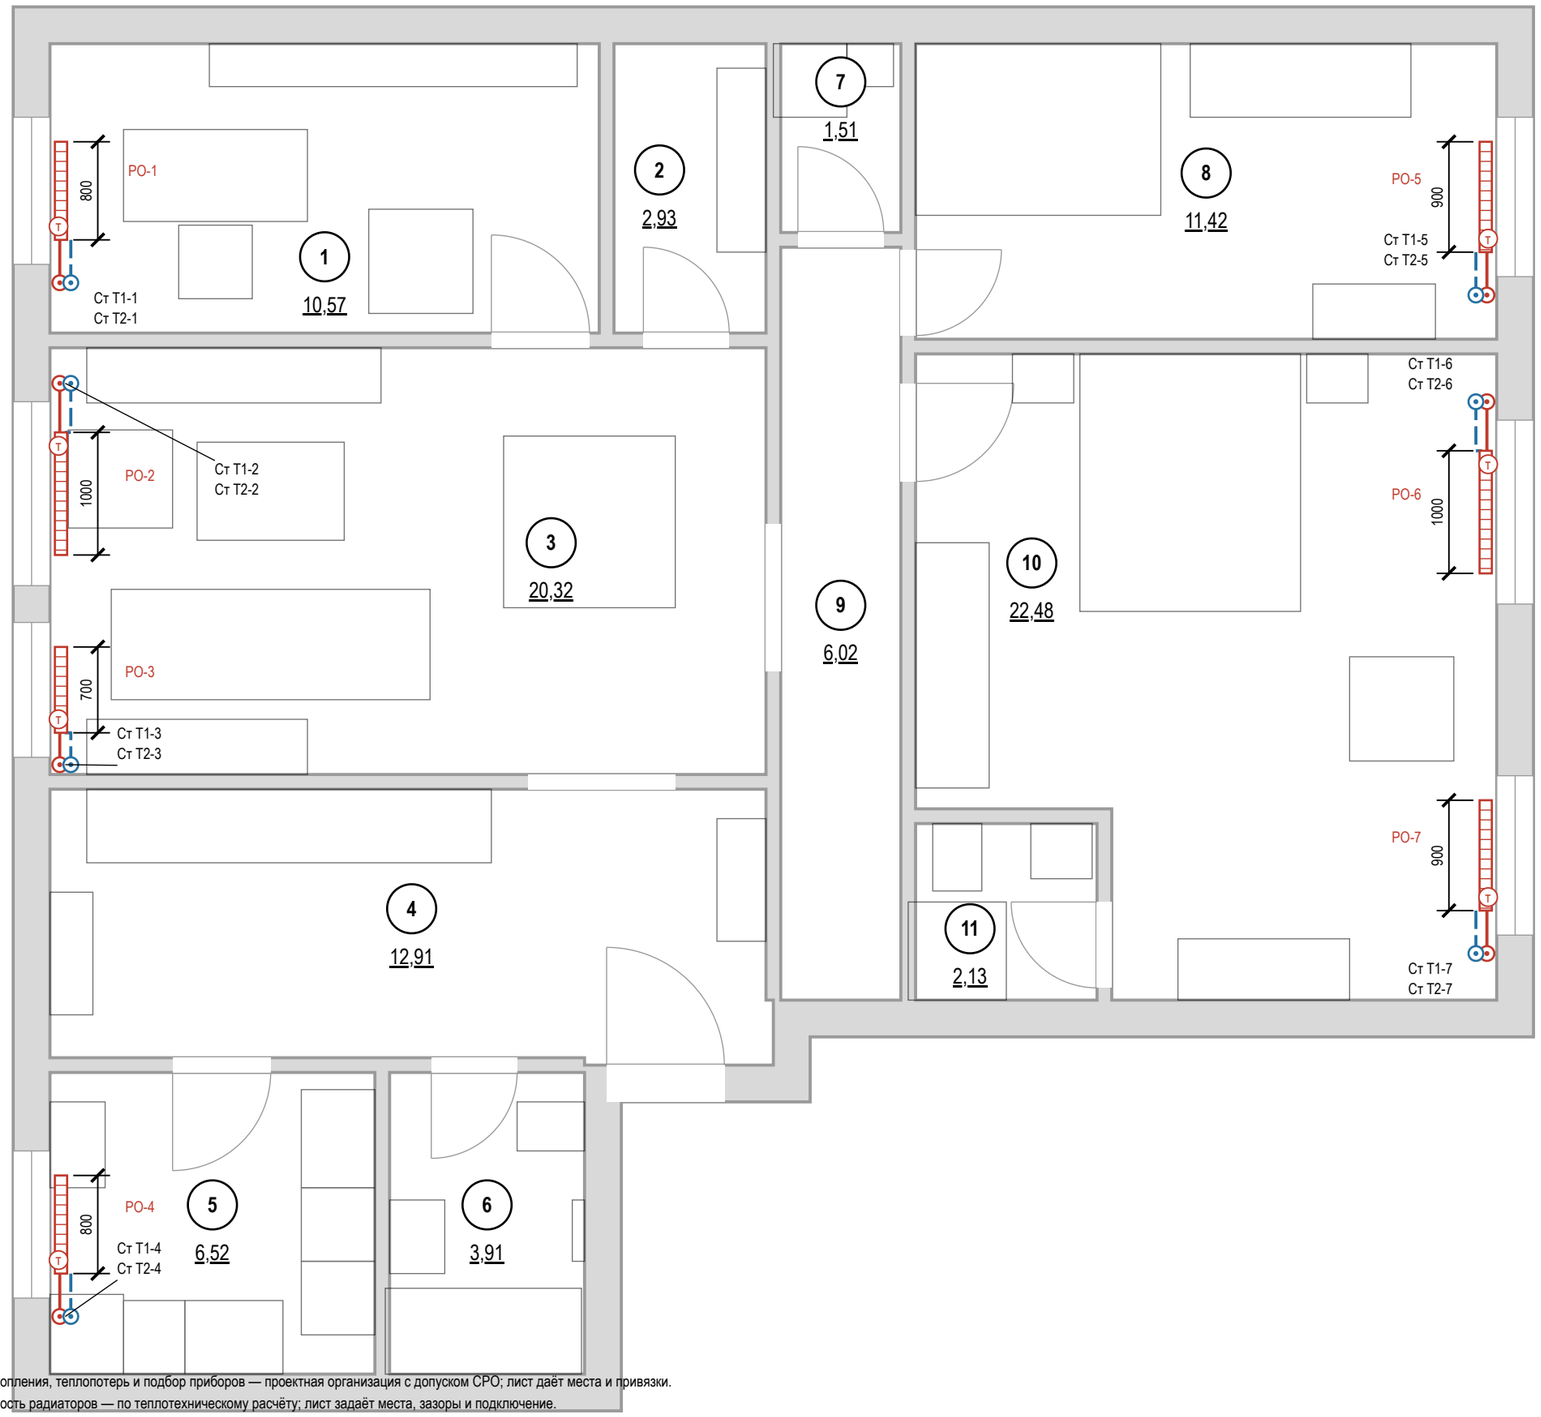

Условные обозначения

- (1) — номер помещения, площадь м²
- радиатор отопления (марка РО-N, длина по плану)
- (Т) — клапан с термоголовкой на подаче
- стояк отопления, подающий (Ст Т1-N)
- стояк отопления, обратный (Ст Т2-N)
- Т1 — отопление, подающий трубопровод
- Т2 — отопление, обратный трубопровод

Ведомость радиаторов

Марка	Помещение	Тип	Д×В×Г, мм	Низ / стена	Q, Вт
РО-1	1. Кабинет-библиотека	панельный	800×400×100	120 / 40	расч.
РО-2	3. Гостиная-столовая	панельный	1000×400×100	120 / 40	расч.
РО-3	3. Гостиная-столовая	панельный	700×400×100	120 / 40	расч.
РО-4	5. Кухня	панельный	800×500×100	120 / 40	расч.
РО-5	8. Спальня 2	панельный	900×500×100	120 / 40	расч.
РО-6	10. Спальня мастер	панельный	1000×500×100	120 / 40	расч.
РО-7	10. Спальня мастер	панельный	900×500×100	120 / 40	расч.

тип и мощность — по теплотехническому расчёту
Низ — от чистого пола, стена — зазор до задней панели, мм.

Привязки — до обмера


Стояки отопления в исходных данных не заданы: показаны у откосов окон, подводки — принципиально. До черновых работ — обмер стояков и паспорта приборов; лист перевыпустить по факту.

Примечания

1. Расчёт системы отопления, теплопотерь и подбор приборов — проектная организация с допуском СРО; лист даёт места и привязки.
2. Тип, длина и мощность радиаторов — по теплотехническому расчёту; лист задаёт места, зазоры и подключение.
3. Радиаторы — под каждым окном жилых комнат и кухни, центр по оси проёма, длина 0,7 ширины окна (кратно 100); окончательно — по расчёту.
4. Зазоры радиатора: низ не менее 100 мм от чистого пола, верх не менее 100 мм до подоконника, 30–50 мм от стены до задней панели; центр по оси окна с допуском ±20 мм.
5. Радиаторы не закрывать глухими коробами и мебелью; перенос и замена приборов в многоквартирном доме — переустройство, согласование с управляющей организацией (ЖК РФ ст. 25–26); вынос на лоджию запрещён.
6. Трубы отопления через межквартирные стены не прокладывать (СП 51.13330.2011, п. 9.19); через перекрытия и перегородки — в гильзах.
7. Привязки приборов и подводок — по паспортам приобретённых радиаторов и клапанов, до черновых работ.
8. До закрытия отделкой трубопроводы отопления испытать гидростатическим давлением с оформлением акта (СП 73.13330.2016, 7.2–7.3).

					Проект: Квартира 103 м²
	Лист	№ док.	Подпись	Дата	План отопления
Дизайнер	Кырлан А.С.			18.10.26	Стадия: П; Лист: 28; Листов: 103

выпуск 18.10.2026 № d119044df4 · стр. 28 из 103

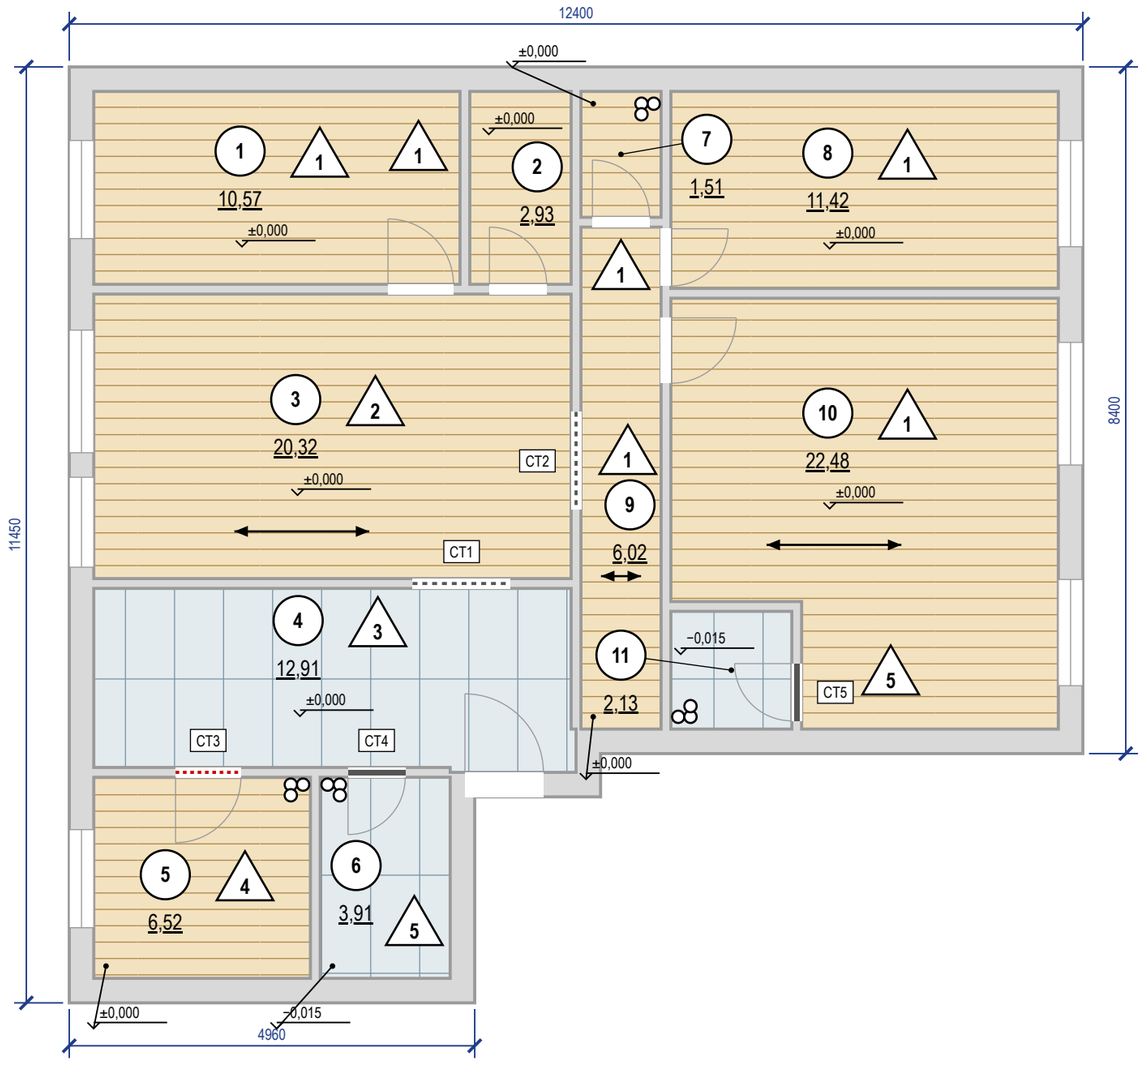

Экспликация полов

Номер помещения	Тип пола	Схема пола	Данные элементов пола (наименование, толщина, основание), мм	Площадь, м²
1, 2, 7, 8, 9, 10	1		Инженерная доска на клею — 14 Стяжка ЦПС М200 — 50 Плита перекрытия Всего 64 мм; ЧП ±0,000, верх плиты −0,064	54,93
3	2		Инженерная доска дуб на клею — 14 Клей паркетный МС-полимерный — 1 Стяжка ЦПС М300 (В22,5), фибра, по звукоизоляции — 55 Звукоизоляция — минплита 110 кг/м³ 20 Засыпка керамзитовая фр. 0–5, уплотнённая — 80 Плита перекрытия монолитная Всего 170 мм; ЧП ±0,000, верх плиты −0,170	20,32
4	3		Керамогранит на клею C2 TE S1 — 14 Стяжка ЦПС М200 — 50 Плита перекрытия Всего 64 мм; ЧП ±0,000, верх плиты −0,064	12,91
5	4		Инженерная доска дуб на клею — 14 Клей паркетный МС-полимерный — 1 Гидроизоляция полиуретановая, 2 слоя (зона мойки и острова) — 2 Стяжка ЦПС М300 (В22,5), фибра, по звукоизоляции — 53 Звукоизоляция — минплита 110 кг/м³ 20 Засыпка керамзитовая фр. 0–5, уплотнённая — 80 Плита перекрытия монолитная Всего 170 мм; ЧП ±0,000, верх плиты −0,170	6,52
6, 11	5		Керамогранит на клею C2 TE S1 — 14 Гидроизоляция обмазочная, 2 слоя, с заведением на стены 200 мм — 2 Стяжка ЦПС М200 — 33 Плита перекрытия Всего 49 мм; ЧП −0,015, верх плиты −0,064	6,04
			Итого	**100,72**

Спецификация плинтусов

Наименование	Помещения	Длина, м (с запасом)
Плинтус МДФ под покраску 80×16, крепление к стене, окраска в цвет Farrow & Ball No. 291	1, 2, 4, 7, 8, 9, 10	88
Плинтус МДФ под окраску 80×16 мм, крепление к стене, окраска в цвет Farrow & Ball No. 291	3, 5	27

Отметки по высоте

±0,000 чистый пол пом. 1–5, 7–10; отсчёт высот
−0,015 чистый пол пом. 6, 11, ниже на 15 мм
плита верх плиты разный: −0,064, −0,170 (задание на обмер)
сущ. пол снимается до плиты; не замерен (задание на обмер)

Примечания


1. За отметку ±0,000 принят чистый пол, не существующий (блок отметок). Площади — по чистым размерам помещений, м²; размеры — в мм.
2. Стык разнотипных покрытий — по оси дверного полотна (под полотном в закрытом положении); решение стыка — по ведомости стыков.
3. Пол санузлов ниже смежных помещений на 15 мм; гидроизоляция по стяжке с заведением на стены не менее 200 мм (СП 29.13330.2011, п. 7.2), до облицовки — тест проливом и акт скрытых работ.
4. Трубопроводы в конструкции пола не прокладываются: пирог пола 49–170 мм не вмещает выпуски канализации с уклоном — выпуски К1 ведутся по стенам над чистым полом в коробах (лист 16).
5. Штучные покрытия (инженерная доска): направление — по стрелке; влажность основания по СМ не более 2,0 % (по ТУ изготовителя).
6. Ровность основания — просвет под 2-метровой рейкой не более 2 мм: пом. 1, 2, 3, 5, 7, 8, 9, 10 (инженерная доска), пом. 4, 6, 11 (керамогранит); проверить до укладки покрытия (СП 71.13330.2017, табл. 8.5).
7. Плавающая стяжка по звукоизоляции: демпферная (кромочная) лента по контуру помещения, у стояков и колонн — до верха чистого пола (СП 51.13330.2011, п. 9.11); плинтус крепится только к стене.
8. Сетка на плитке — условная, в размер формата; точка старта и раскладка — по листу раскладки плитки.
9. Пироги полов — по экспликации полов: слои сверху вниз, толщины в мм; гидроизоляция мокрых зон — в пироге и в ведомости отделки; схема пола — без масштаба.

					Проект: Квартира 103 м²
	Лист	№ док.	Подпись	Дата	План покрытий пола
Дизайнер	Кырлан А.С.			18.10.26	


Стадия	Лист	Листов
П	29	103

выпуск 18.10.2026 № d119044df4 · стр. 29 из 103

Фрагмент 1. Ванная (пом. 6). Пол 600×600, шов 2 мм, М 1:20

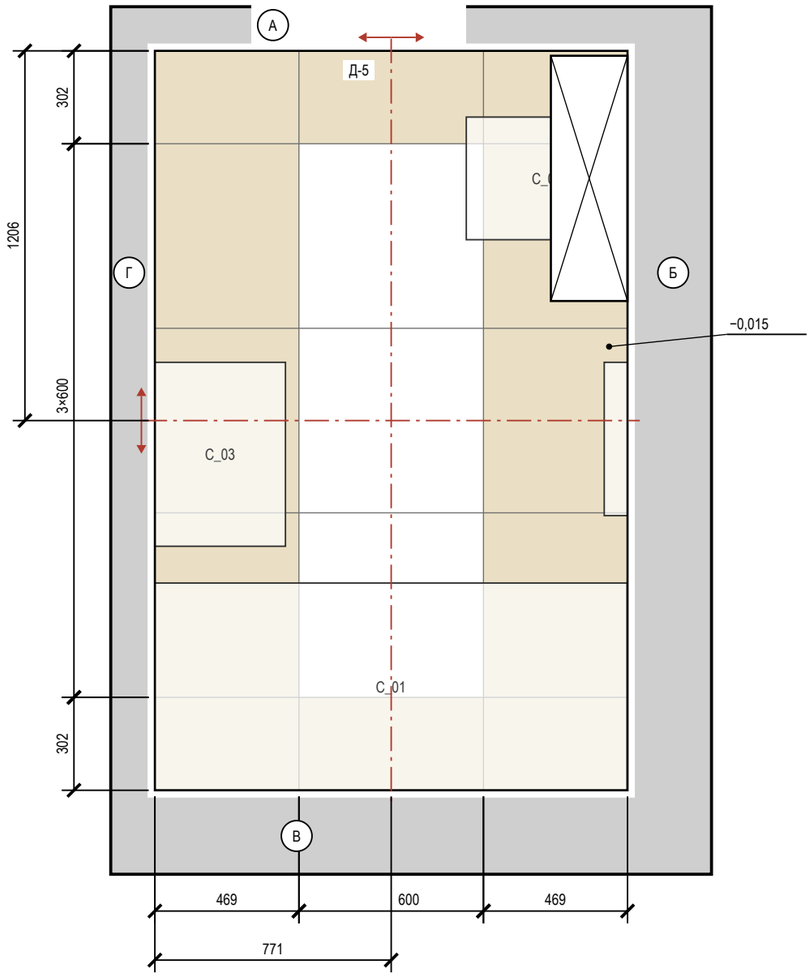

Фрагмент 2. Ванная мастер (пом. 11). Пол 600×600, шов 2 мм, М 1:20

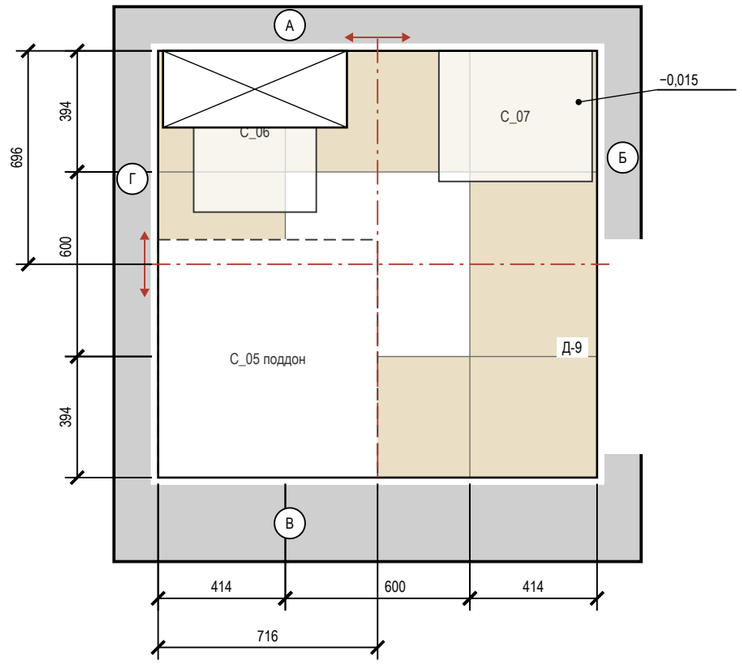

Условные обозначения

- плитка целая; тонкая линия — шов
- плитка с подрезкой (размер — на цепочке)
- ось старта; стрелки — направление укладки
- сантехприбор: габарит, высота по практике
- поддон душа — плитку пола под ним не кладут
- короб инсталляции: плитка пола — до короба
- отметка чистого пола на полке выноски, м
- А — обозначение стены А–Г (как на развёртках)

Ведомость плитки

Помещение, поверхность	Плитка, код	Формат	Шов	S, м²	Целых	Подр.	С запасом
Ванная, пол	аналог: керамогранит под травертин	600×600	2	3,91	3	12	17
Ванная, стены А–Г	аналог: керамогранит под травертин	600×1200	2	17,04	13	19	36
Ванная, короб инсталляции	аналог: керамогранит под травертин	600×1200	2	1,76	0	6	7
Ванная мастер, пол	аналог: керамогранит под травертин	600×600	2	2,13	0	8	9
Ванная мастер, стены А–Г	аналог: керамогранит под травертин	600×1200	2	11,85	5	19	28
Ванная мастер, короб инсталляции	аналог: керамогранит под травертин	600×1200	2	1,47	1	3	5
Прихожая-холл, пол	A8UZ	600×1200	2	12,91	0	20	22
Итого 600×600				6,04	3	20	26
Итого 600×1200				**45,03**	**19**	**67**	**98**

Примечания

1. Раскладка от чистовых размеров: стены санузлов теряют 10 + 5 + 9 = 24 мм на сторону (штукатурка, клей, плитка); подрезки — чистые, без шва.
2. Старт — от центра помещения (штрихпунктир, стрелки направление укладки); размер старта — от чистовых стен Г и А.
3. Раскладка пола «Прихожая-холл» — на листе «Раскладка плитки. Прихожая-холл».
4. Калибр партии не задан — до укладки замерить (рабочий размер W, ГОСТ 13996-2019) и пересчитать подрезки.
5. Количество: целые по раскладке + по одной на подрезку, запас 10 %; один артикул — одна партия и тон. Исключены поддон, короб, проёмы и места за коробом; S — по чистым граням: стены нетто = зона облицовки по ведомости отделки − место за коробом инсталляции 1,68 м² (плитку за коробом не кладут), короб — отдельной строкой.
6. Клей C2 TE S1 Ceresit CM 17; C2 TE S1 (ГОСТ Р 56387-2018), затирка CG2WA Mapei Ultracolor Plus 132; CG2WA; расход — по ТУ выбранной марки.
7. Гидроизоляция: пол и стены 200 мм от ЧП; над ванной до 2000 и 300 мм за борт, у душа — до 2000 и 500 мм за поддон (см. развёртки); акт скрытых работ, пролив 24 ч.
8. Швы пола совмещены со швами стены А; по периметру демпферная лента.
9. Отметка чистого пола −0,015, порог 15 мм; стык с соседним покрытием — по оси полотна двери.


Ведомость материалов

Материал	Класс, код	Норма расхода	Кол-во
Затирка	CG2WA Mapei Ultracolor Plus 132	(a+b)/ab·шов·t·1,6	3,0 кг
Затирка	CG2WA	(a+b)/ab·шов·t·1,6	1,0 кг
Клей	C2 TE S1 Ceresit CM 17	1,5 кг/м²·мм, слой 5	298 кг (12 меш.)
Клей	C2 TE S1	1,5 кг/м²·мм, слой 5	108 кг (5 меш.)
Гидроизоляция	обмазочная, 2 слоя: пол, стены по периметру и зоны замачивания	по ТУ	21,5 м²
Демпф. лента	по периметру пола из плитки		27,1 м

					Проект: Квартира 103 м²
	Лист	№ док.	Подпись	Дата	Раскладка плитки. Планы полов
Дизайнер	Кырлан А.С.			18.10.26	Стадия: П; Лист: 30; Листов: 103

выпуск 18.10.2026 № d119044df4 · стр. 30 из 103

Фрагмент 1. Прихожая-холл (пом. 4). Пол 600×1200, шов 2 мм, М 1:20

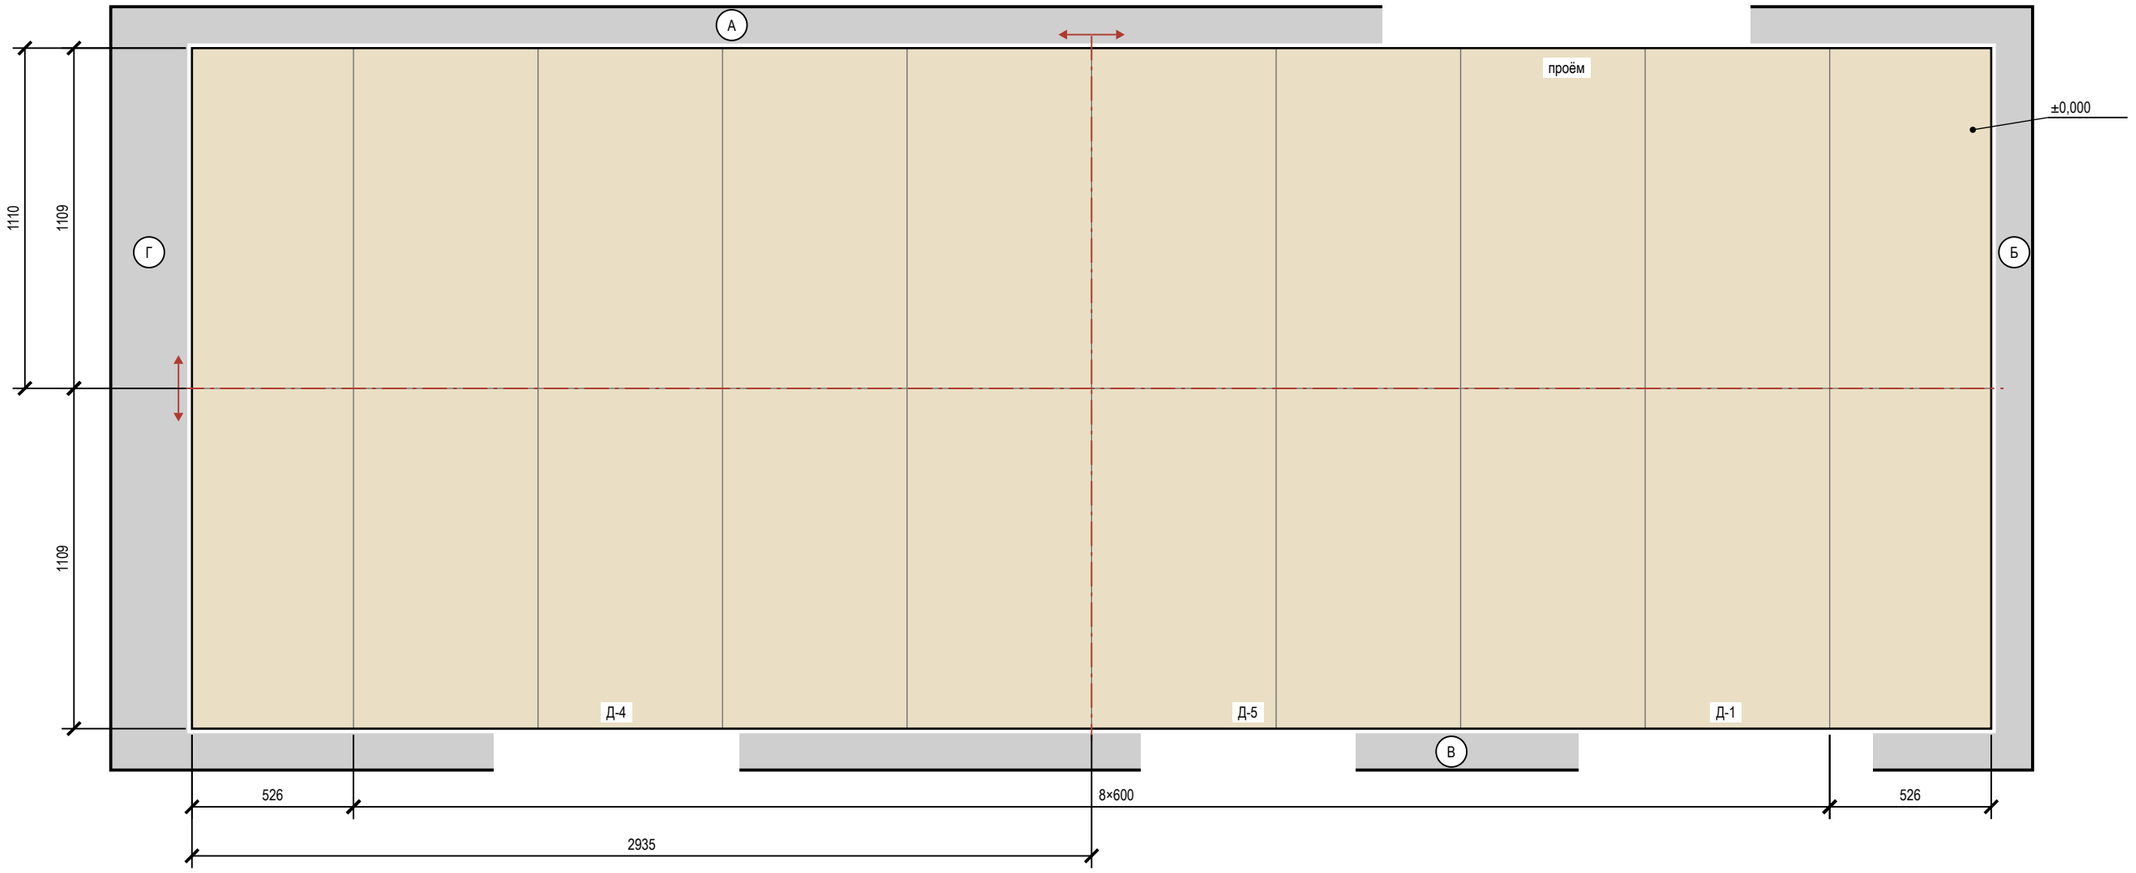

Условные обозначения

- плитка целая; тонкая линия — шов
- плитка с подрезкой (размер — на цепочке)
- ось старта; стрелки — направление укладки
- отметка чистого пола на полке выноски, м
- (А) обозначение стены А–Г (как на развёртках)

Подсчёт плитки

Поверхность	Формат	S, м²	Целых	Подр.	С запасом
Прихожая-холл, пол	600×1200	12,91	0	20	22

Примечания

1. Прихожая-холл: керамогранит 600×1200, длинная сторона — вдоль стен Б и Г, шов 2 мм, прямая раскладка от центра. Стены окрашены: раскладка от чистового контура минус штукатурка и шпаклёвка 15 мм на сторону (принято); подрезки 526 / 1109 мм, срез — под плинтус.
2. Прихожая-холл: деформационный зазор по периметру 8–10 мм под плинтусом; в проёмах — стык с соседним покрытием по оси полотна двери. Клей C2 TE S1, затирка CG2WA.
3. Клей, затирка и итог по форматам — в ведомостях листа «Раскладка плитки. Планы полов».

					Проект: Квартира 103 м²
	Лист	№ док.	Подпись	Дата	
Дизайнер	Кырлан А.С.			18.10.26	Раскладка плитки. Прихожая-холл

Стадия	Лист	Листов
П	31	103

выпуск 18.10.2026 № d119044df4 · стр. 31 из 103



					Проект: Квартира 103 м²	
	Лист	№ док.	Подпись	Дата	Визуализация. Вид сверху	Стадия / Лист / Листов
Дизайнер	Кырлан А.С.			18.10.26		П / 32 / 103

выпуск 18.10.2026 № d119044df4 · стр. 32 из 103



					Проект: Квартира 103 м²	
	Лист	№ док.	Подпись	Дата		
Дизайнер	Кырлан А.С.			18.10.26	Визуализация: Кабинет-библиотека	Стадия / Лист / Листов
						П / 33 / 103

выпуск 18.10.2026 № d119044df4 · стр. 33 из 103



					Проект: Квартира 103 м²
	Лист	№ док.	Подпись	Дата	Визуализация: Кабинет-библиотека
Дизайнер	Кырлан А.С.			18.10.26	

Стадия	Лист	Листов
П	34	103

выпуск 18.10.2026 · d119044df4 · стр. 34 из 103



					Проект: Квартира 103 м²	
	Лист	№ док.	Подпись	Дата		
Дизайнер	Кырлан А.С.			18.10.26	Визуализация: Кабинет-библиотека	Стадия / Лист / Листов
						П / 35 / 103

выпуск 18.10.2026 № d119044df4 · стр. 35 из 103

Развёртка стены А


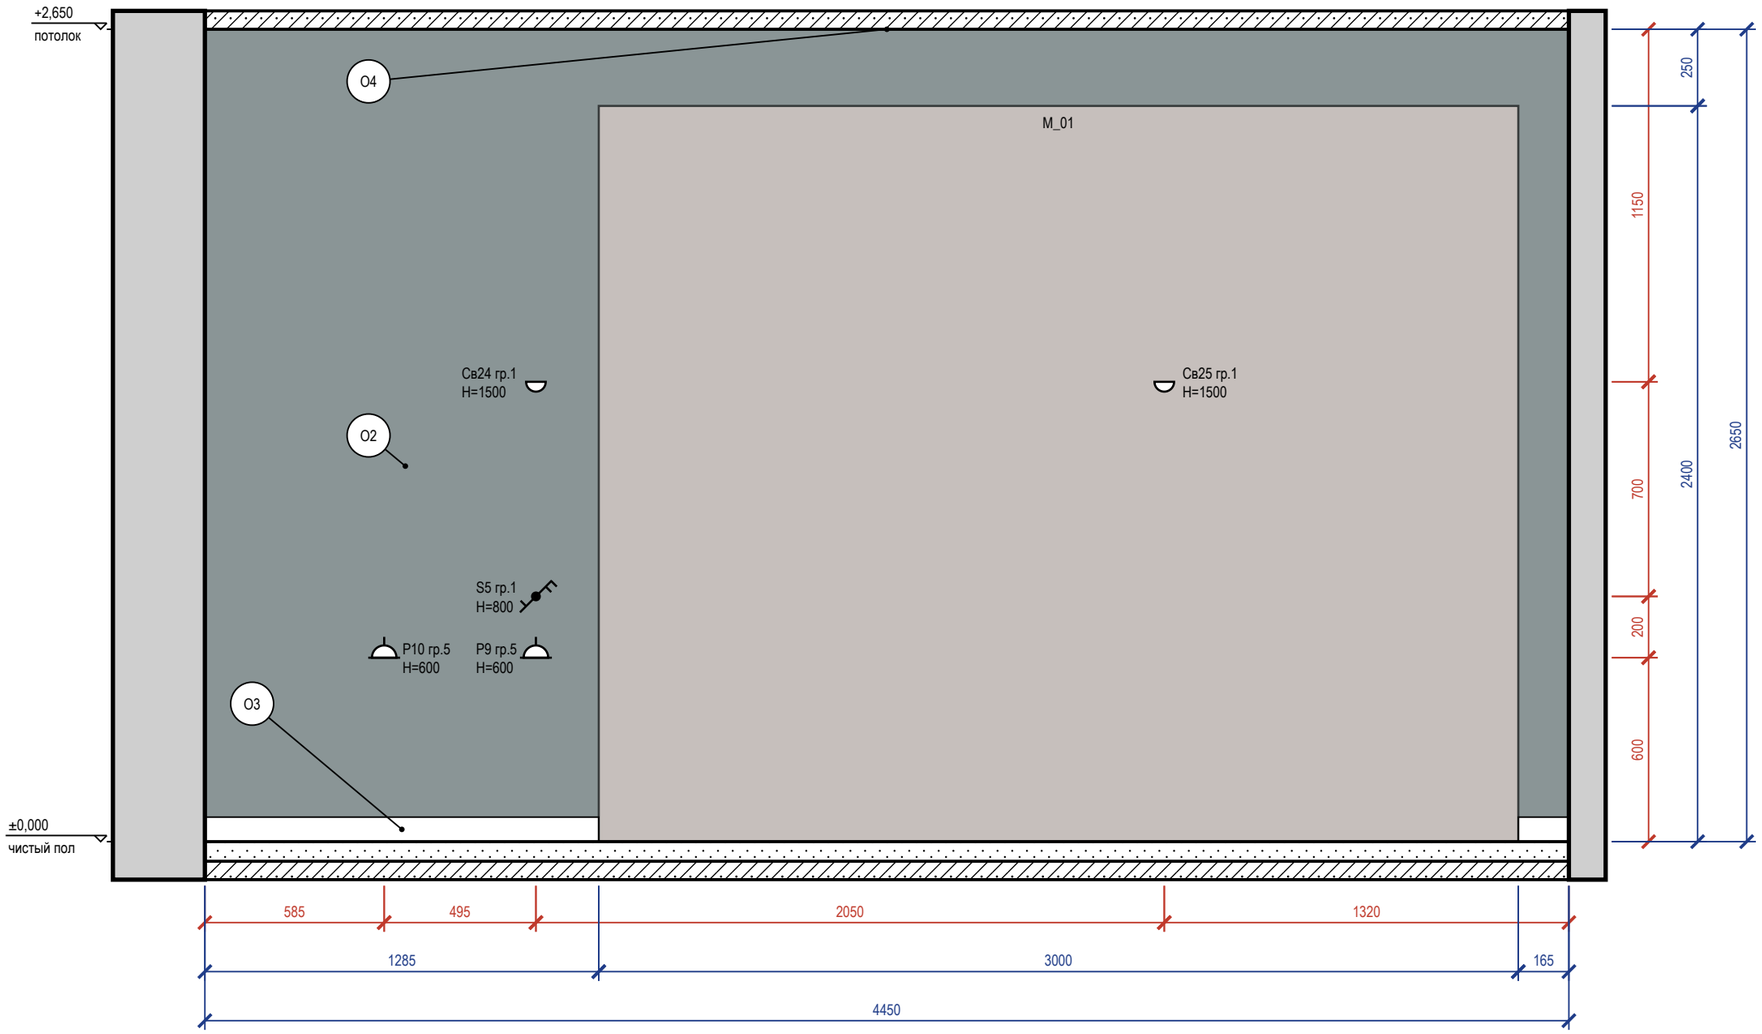



Схема развёрток (М 1:100)

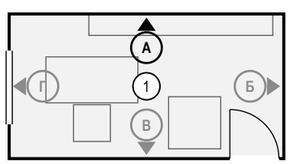

Ведомость отделки (на листе)

Марка	Поверхность	Материал, изделие	Цвет, код	Кол.
О2	акцентная стена	окраска, Farrow & Ball Modern Emulsion, матовая, подготовка Q3	Farrow & Ball No. 289 «Inchyra Blue — тёмный сине-серый»	11,8 м²
О3	плинтус	плинтус МДФ, h 80 мм, аналог: плинтус МДФ под покраску 80×16	Farrow & Ball No. 291 «School House White тёплый меловой белый»	1,4 м
О4	потолок	окраска, Tikkurila Anti-Reflex 2, глубокоматовая, подготовка Q3	NCS S 0502-Y «Белый с лёгкой желтизной»	10,6 м²

Визуализация этой стены — лист 33

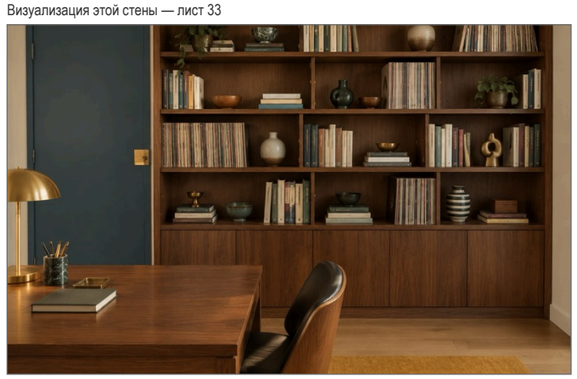

Примечания

1. Размеры — в мм от чистовых поверхностей стен; условные обозначения и общие указания — лист 2.

					Проект: Квартира 103 м²
	Лист	№ док.	Подпись	Дата	
Дизайнер	Кырлан А.С.			18.10.26	Развёртка стены А. Кабинет-библиотека (пом. 1)

Стадия	Лист	Листов
П	36	103

выпуск 18.10.2026 № d119044df4 · стр. 36 из 103

Развёртка стены Б


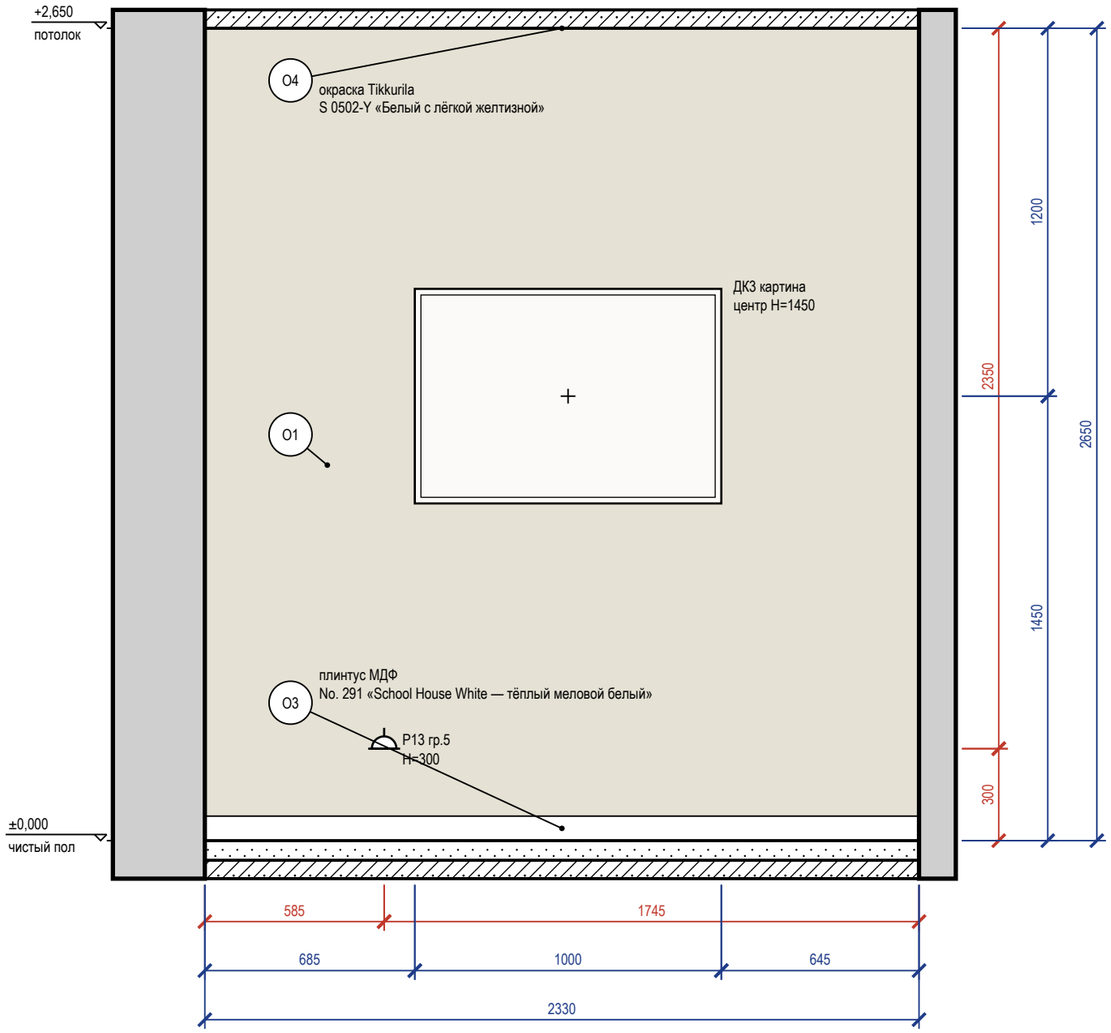


Схема развёрток (М 1:100)

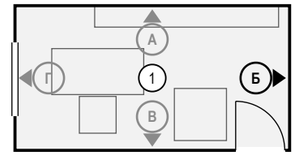

Ведомость отделки (на листе)

Марка	Поверхность	Материал, изделие	Цвет, код	Кол.
О1	стены	окраска, Farrow & Ball Modern Emulsion, матовая, подготовка Q3	Farrow & Ball No. 291 «School House White — тёплый меловой белый»	6,2 м²
О3	плинтус	плинтус МДФ, h 80 мм, аналог: плинтус МДФ под покраску 80×16	Farrow & Ball No. 291 «School House White — тёплый меловой белый»	2,3 м
О4	потолок	окраска, Tikkurila Anti-Reflex 2, глубокоматовая, подготовка Q3	NCS S 0502-Y «Белый с лёгкой желтизной»	10,6 м²

Визуализация этой стены — лист 34



Примечания

1. Размеры — в мм от чистовых поверхностей стен; условные обозначения и общие указания — лист 2.
2. Картины и зеркала крепить к основанию по паспорту изделия (закладные и анкеры — в перечне скрытых работ); крест — ось центра предмета.

					Проект: Квартира 103 м²			
	Лист	№ док.	Подпись	Дата	Развёртка стены Б. Кабинет-библиотека (пом. 1)	Стадия	Лист	Листов
Дизайнер	Кырлан А.С.			18.10.26		П	37	103

выпуск 18.10.2026 № d119044df4 · стр. 37 из 103

Развёртка стены В


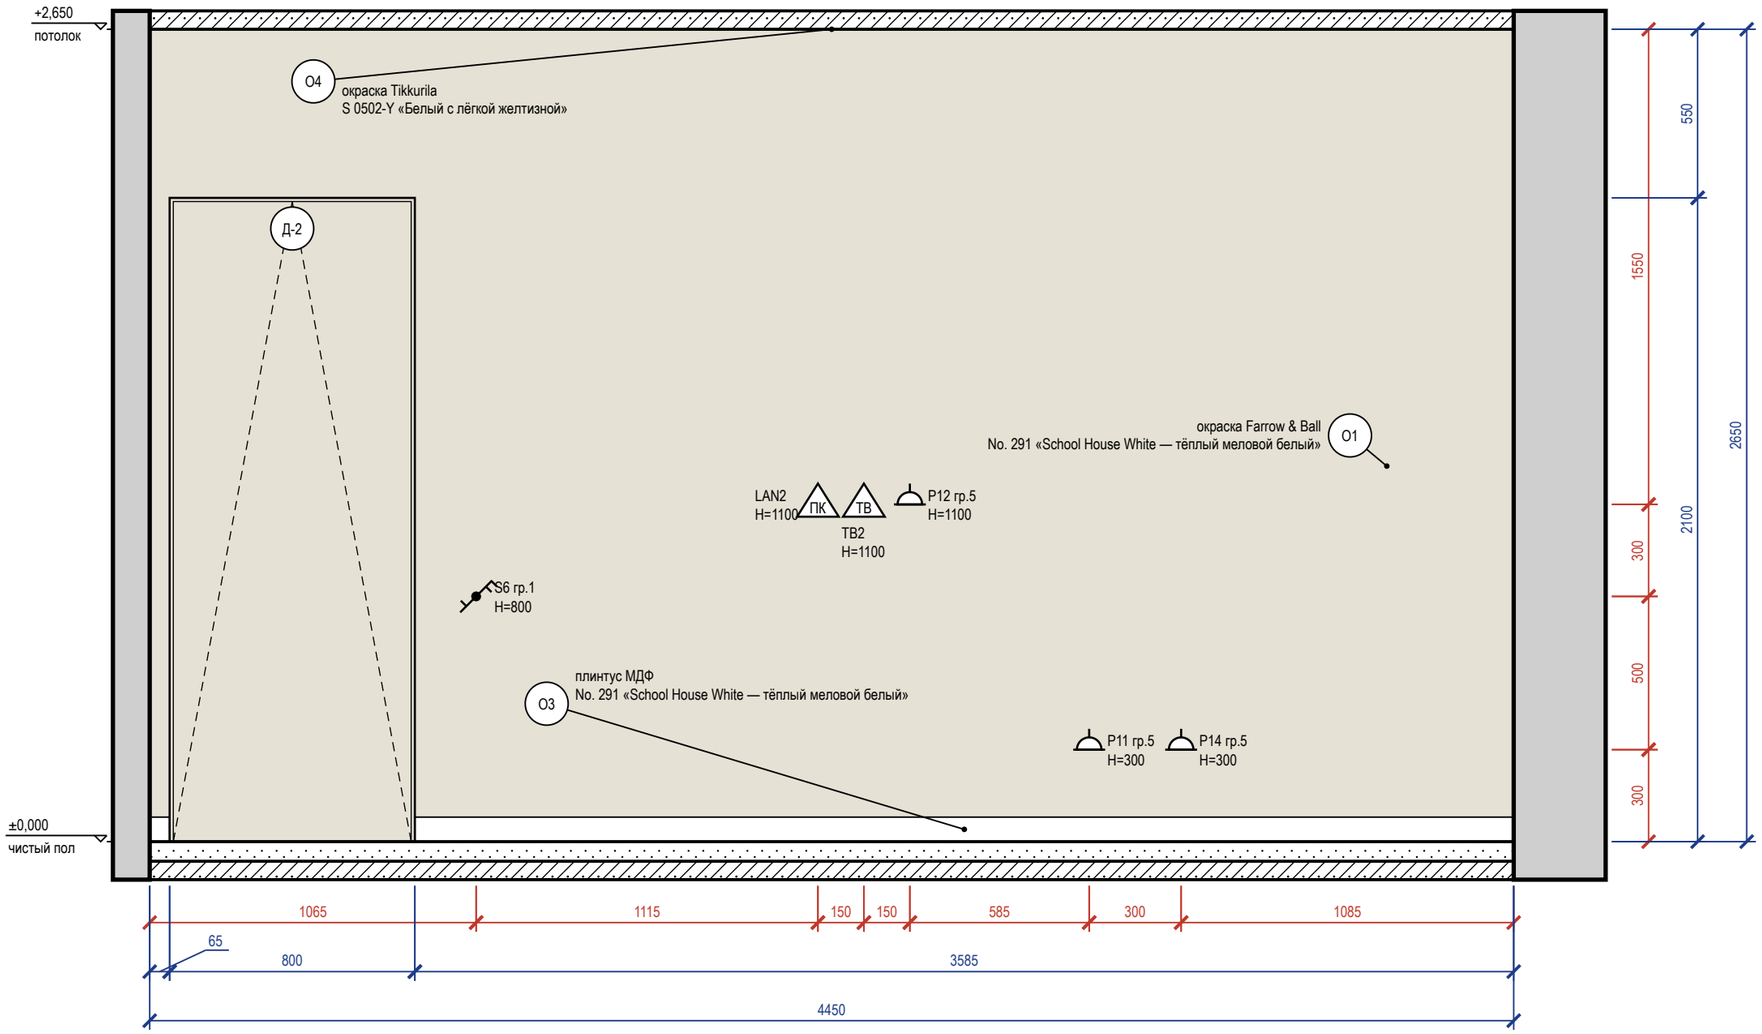


Схема развёрток (М 1:100)

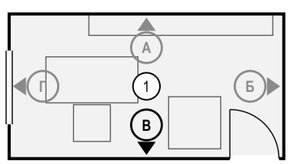

Ведомость отделки (на листе)

Марка	Поверхность	Материал, изделие	Цвет, код	Кол.
О1	стены	окраска, Farrow & Ball Modern Emulsion, матовая, подготовка Q3	Farrow & Ball No. 291 «School House White тёплый меловой белый»	10,1 м²
О3	плинтус	плинтус МДФ, h 80 мм, аналог: плинтус МДФ под покраску 80×16	Farrow & Ball No. 291 «School House White тёплый меловой белый»	3,6 м
О4	потолок	окраска, Tikkurila Anti-Reflex 2, глубокоматовая, подготовка Q3	NCS S 0502-Y «Белый с лёгкой желтизной»	10,6 м²

Примечания

1. Размеры — в мм от чистовых поверхностей стен; условные обозначения и общие указания — лист 2.
2. Двери скрытого монтажа — полотно в плоскости стены, отделка стены по полотну, плинтус прерывается у короба (узел — на листе узлов).

					Проект: Квартира 103 м²
	Лист	№ док.	Подпись	Дата	Развёртка стены В. Кабинет-библиотека (пом. 1)
Дизайнер	Кырлан А.С.			18.10.26	

Стадия	Лист	Листов
П	38	103

выпуск 18.10.2026 № d119044df4 · стр. 38 из 103

Развёртка стены Г


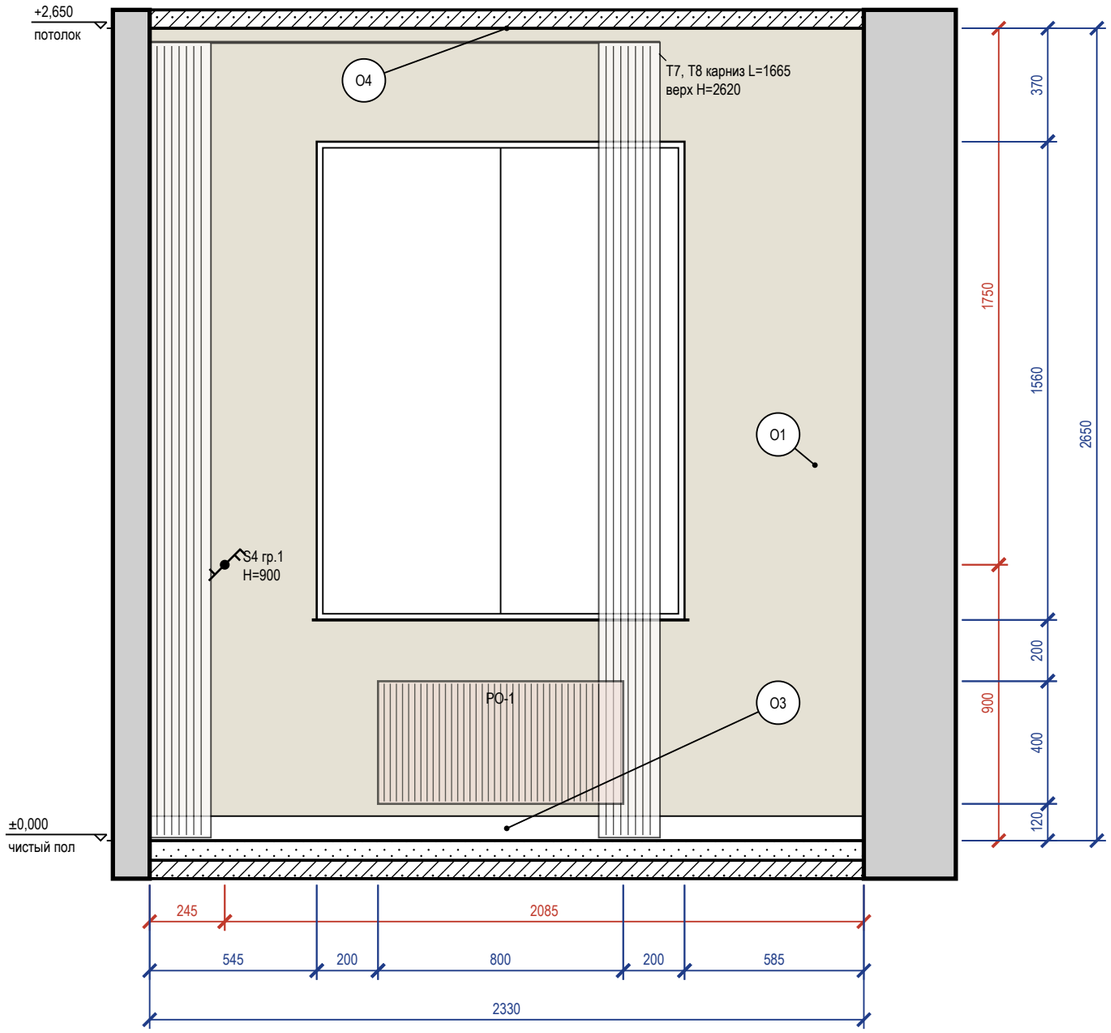


Схема развёрток (М 1:100)

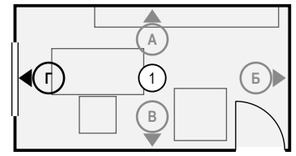

Ведомость отделки (на листе)

Марка	Поверхность	Материал, изделие	Цвет, код	Кол.
О1	стены	окраска, Farrow & Ball Modern Emulsion, матовая, подготовка Q3	Farrow & Ball No. 291 «School House White — тёплый меловой белый»	4,3 м²
О3	плинтус	плинтус МДФ, h 80 мм, аналог: плинтус МДФ под покраску 80×16	Farrow & Ball No. 291 «School House White — тёплый меловой белый»	2,3 м
О4	потолок	окраска, Tikkurila Anti-Reflex 2, глубокоматовая, подготовка Q3	NCS S 0502-Y «Белый с лёгкой желтизной»	10,6 м²

Визуализация этой стены — лист 35



Примечания

1. Размеры — в мм от чистовых поверхностей стен; условные обозначения и общие указания — лист 2.
2. Карнизы (шины) — по ведомости текстиля декоратора; длина L и верх H — по развёртке, крепление — до окраски потолка.
3. Линии узора (швы плитки, складки штор, рёбра радиаторов) прерываются у знаков и выносок — просвет между линиями не менее 0,7 мм.

					Проект: Квартира 103 м²
	Лист	№ док.	Подпись	Дата	Развёртка стены Г. Кабинет-библиотека (пом. 1)
Дизайнер	Кырлан А.С.			18.10.26	

Стадия	Лист	Листов
П	39	103

выпуск 18.10.2026 № d119044df4 · стр. 39 из 103




					Проект: Квартира 103 м²
	Лист	№ док.	Подпись	Дата	
Дизайнер	Кырлан А.С.			18.10.26	Визуализация кладовой

Стадия	Лист	Листов
П	40	103

выпуск 18.10.2026 № d119044df4 · стр. 40 из 103

Развёртка стены Б

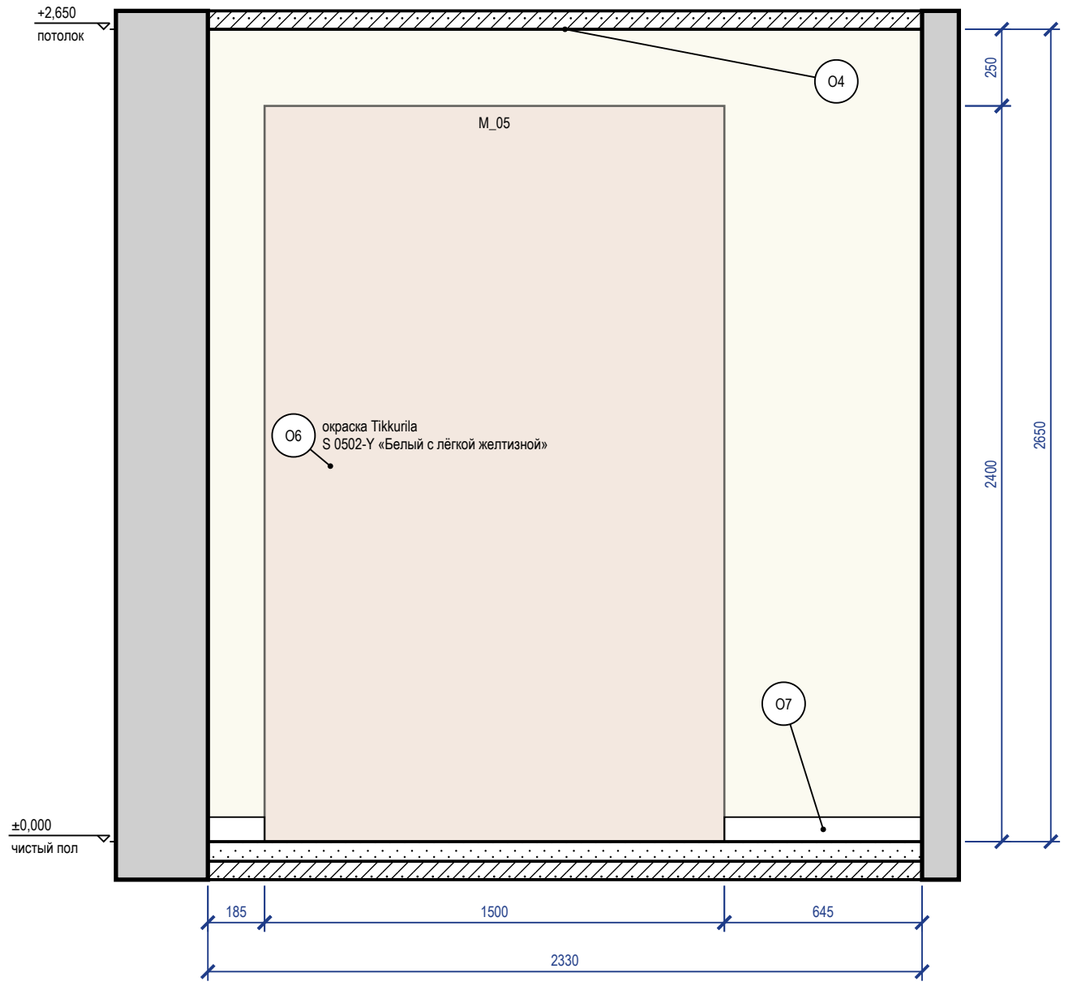

Развёртка стены В


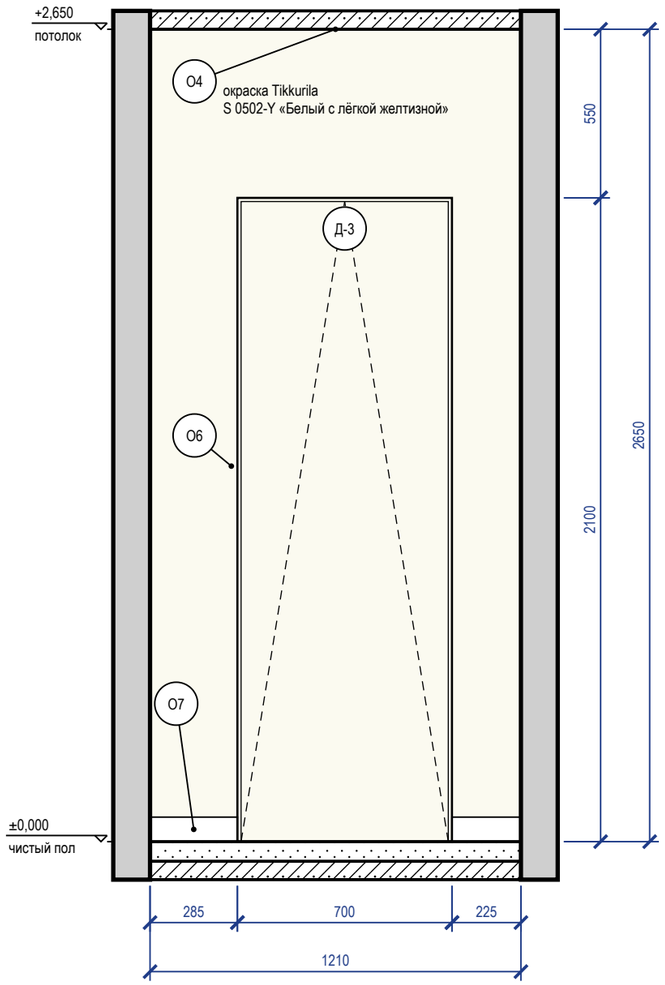


Схема развёрток (М 1:100)

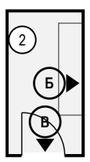

Ведомость отделки (на листе)

Марка	Поверхность	Материал, изделие	Цвет, код	Кол.
О4	потолок	окраска, Tikkurila Anti-Reflex 2, глубокоматовая, подготовка Q3	NCS S 0502-Y «Белый с лёгкой желтизной»	2,9 м²
О6	стены	окраска, Tikkurila Harmony, матовая, подготовка Q3	NCS S 0502-Y «Белый с лёгкой желтизной»	7,9 м²
О7	плинтус	плинтус МДФ, h 80 мм, аналог: плинтус МДФ под покраску 80×16	NCS S 0502-Y «Белый с лёгкой желтизной»	1,3 м

Примечания

1. Размеры — в мм от чистовых поверхностей стен; условные обозначения и общие указания — лист 2.
2. Двери скрытого монтажа — полотно в плоскости стены, отделка стены по полотну, плинтус прерывается у короба (узел — на листе узлов).

					Проект: Квартира 103 м²
	Лист	№ док.	Подпись	Дата	
Дизайнер	Кырлан А.С.			18.10.26	Развёртки стен. Кладовая (пом. 2)
					Стадия: П; Лист: 41; Листов: 103

выпуск 18.10.2026 № d119044df4 · стр. 41 из 103



					Проект: Квартира 103 м²	
	Лист	№ док.	Подпись	Дата		
Дизайнер	Кырлан А.С.			18.10.26	Визуализация: Гостиная-столовая	Стадия / Лист / Листов
						П / 42 / 103

выпуск 18.10.2026 № d119044df4 · стр. 42 из 103



					Проект: Квартира 103 м²			
	Лист	№ док.	Подпись	Дата				
Дизайнер	Кырлан А.С.			18.10.26	Визуализация: Гостиная-столовая	Стадия	Лист	Листов
						П	43	103

выпуск 18.10.2026 № d119044df4 · стр. 43 из 103



					Проект: Квартира 103 м²
	Лист	№ док.	Подпись	Дата	
Дизайнер	Кырлан А.С.			18.10.26	Визуализация: Гостиная-столовая

Стадия	Лист	Листов
П	44	103

выпуск 18.10.2026 № d119044df4 · стр. 44 из 103



					Проект: Квартира 103 м²
	Лист	№ док.	Подпись	Дата	
Дизайнер	Кырлан А.С.			18.10.26	Визуализация: Гостиная-столовая

Стадия	Лист	Листов
П	45	103

выпуск 18.10.2026 № d119044df4 · стр. 45 из 103

Развёртка стены А


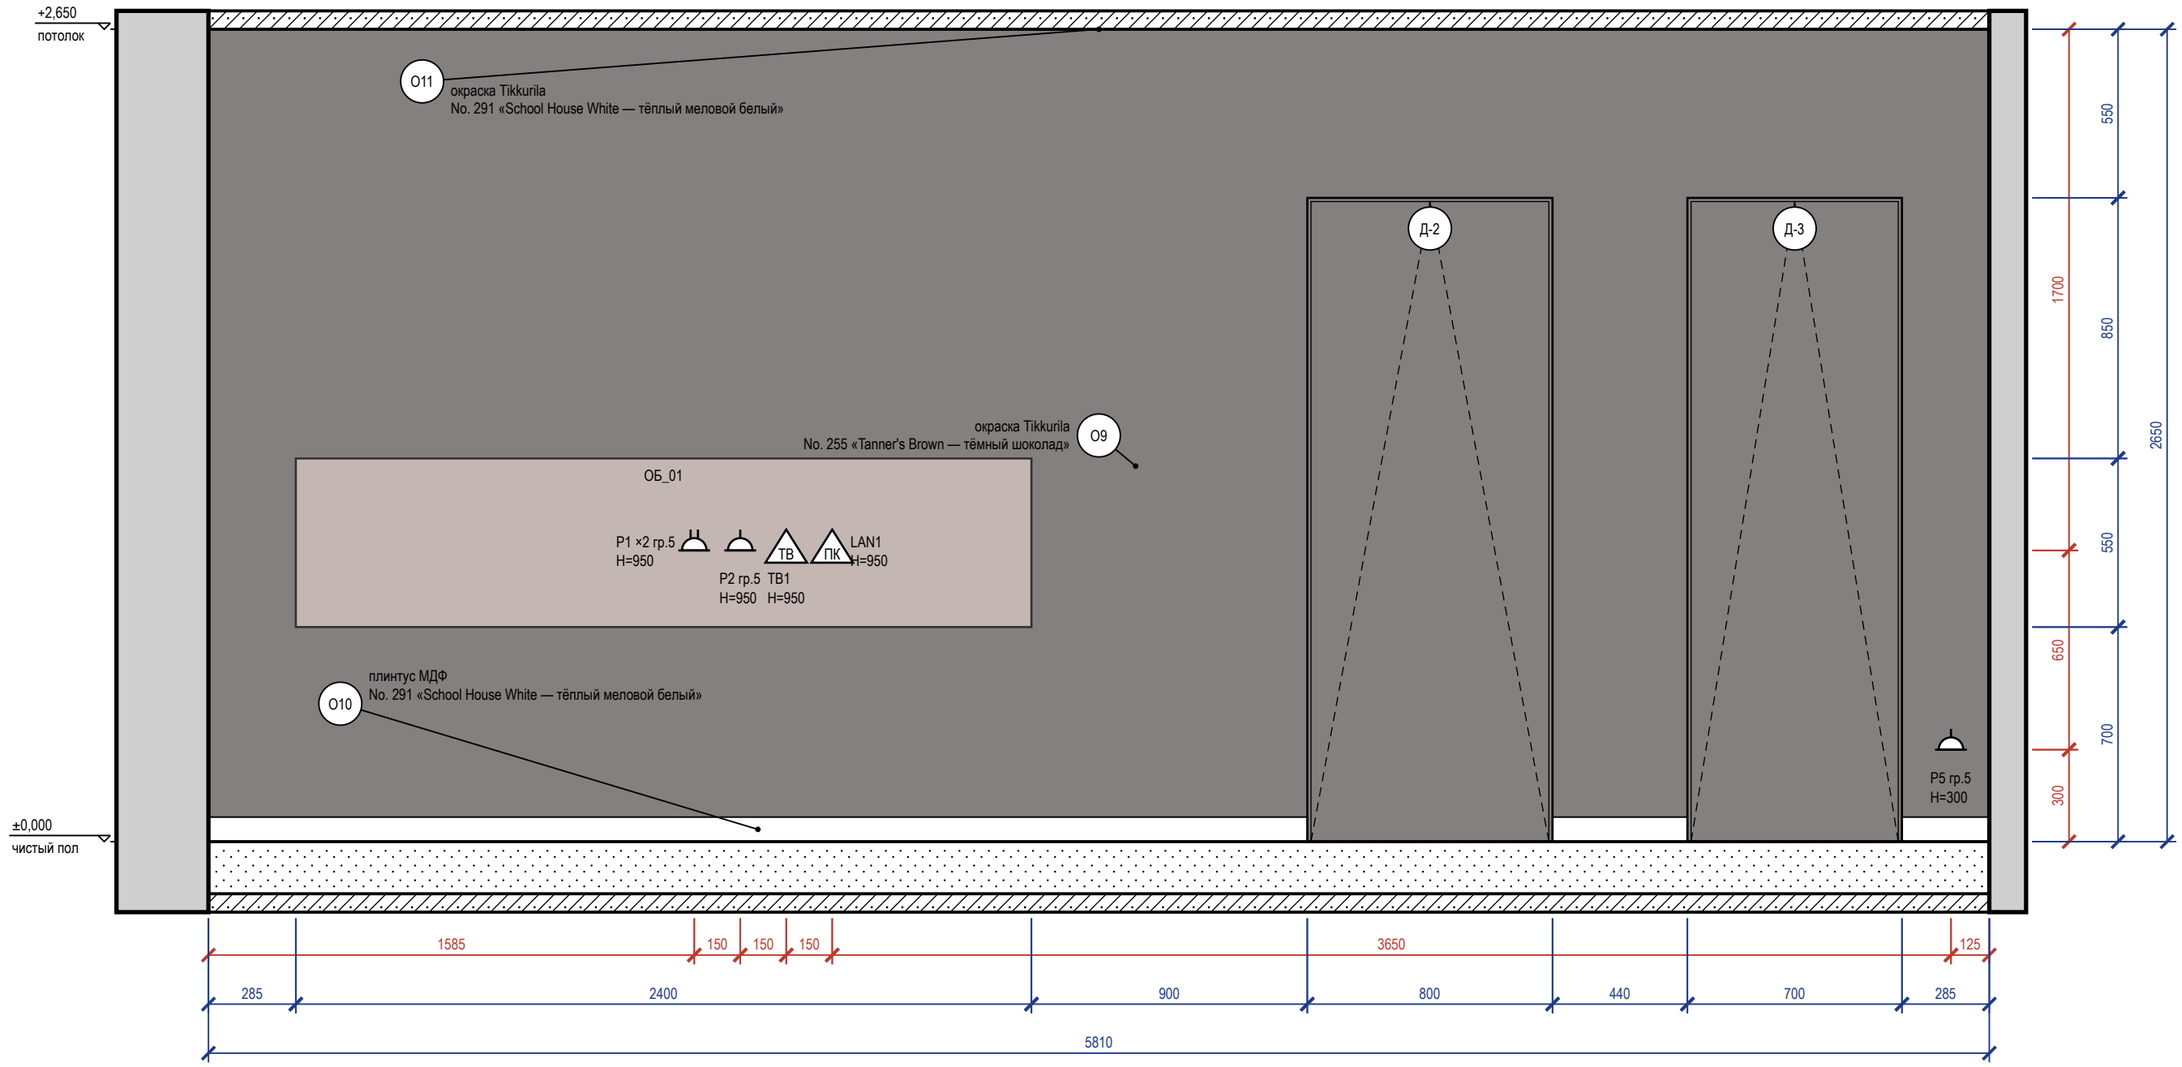



Схема развёрток (М 1:100)

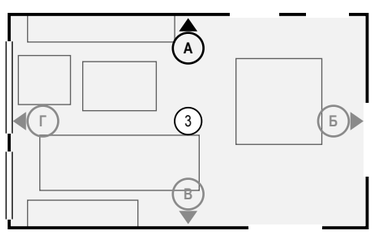

Ведомость отделки (на листе)

Марка	Поверхность	Материал, изделие	Цвет, код	Кол.
О9	акцентная стена	окраска, Tikkurila Optiva 5 Matt, аналог: интерьерная краска, класс 2 по EN 13300, глубокоматовая/матовая, база С, матовая, подготовка К3	Farrow & Ball No. 255 «Tanner's Brown — тёмный шоколад»	12,2 м²
О10	плинтус	плинтус МДФ, h 80 мм, аналог: плинтус МДФ под окраску 80×16 мм, полуглянцевая	Farrow & Ball No. 291 «School House White тёплый меловой белый»	4,3 м
О11	потолок	окраска, Tikkurila Anti-Reflex 2, глубокоматовая, подготовка Q3	Farrow & Ball No. 291 «School House White тёплый меловой белый»	20,3 м²

Визуализация этой стены — лист 42

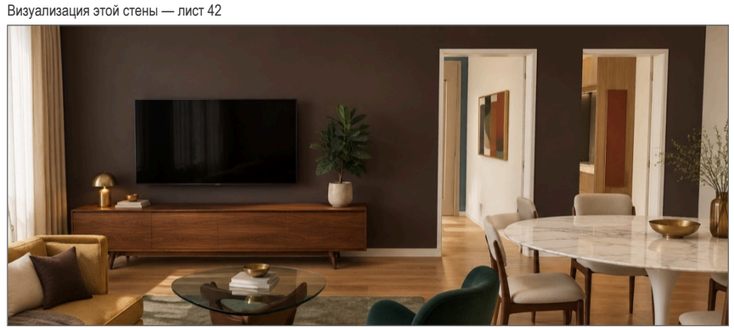

Примечания

1. Размеры — в мм от чистовых поверхностей стен; условные обозначения и общие указания — лист 2.
2. Схема мебели, приборов и декора не является технической документацией для производства мебели; габариты — по паспортам изделий.
3. Двери скрытого монтажа — полотно в плоскости стены, отделка стены по полотну, плинтус прерывается у короба (узел — на листе узлов).

	Лист	№ док.	Подпись	Дата
Дизайнер	Кырлан А.С.			18.10.26

Проект: Квартира 103 м²

Развёртка стены А.
Гостиная-столовая (пом. 3)

Стадия	Лист	Листов
П	46	103

выпуск 18.10.2026 № d119044df4 · стр. 46 из 103

Развёртка стены Б


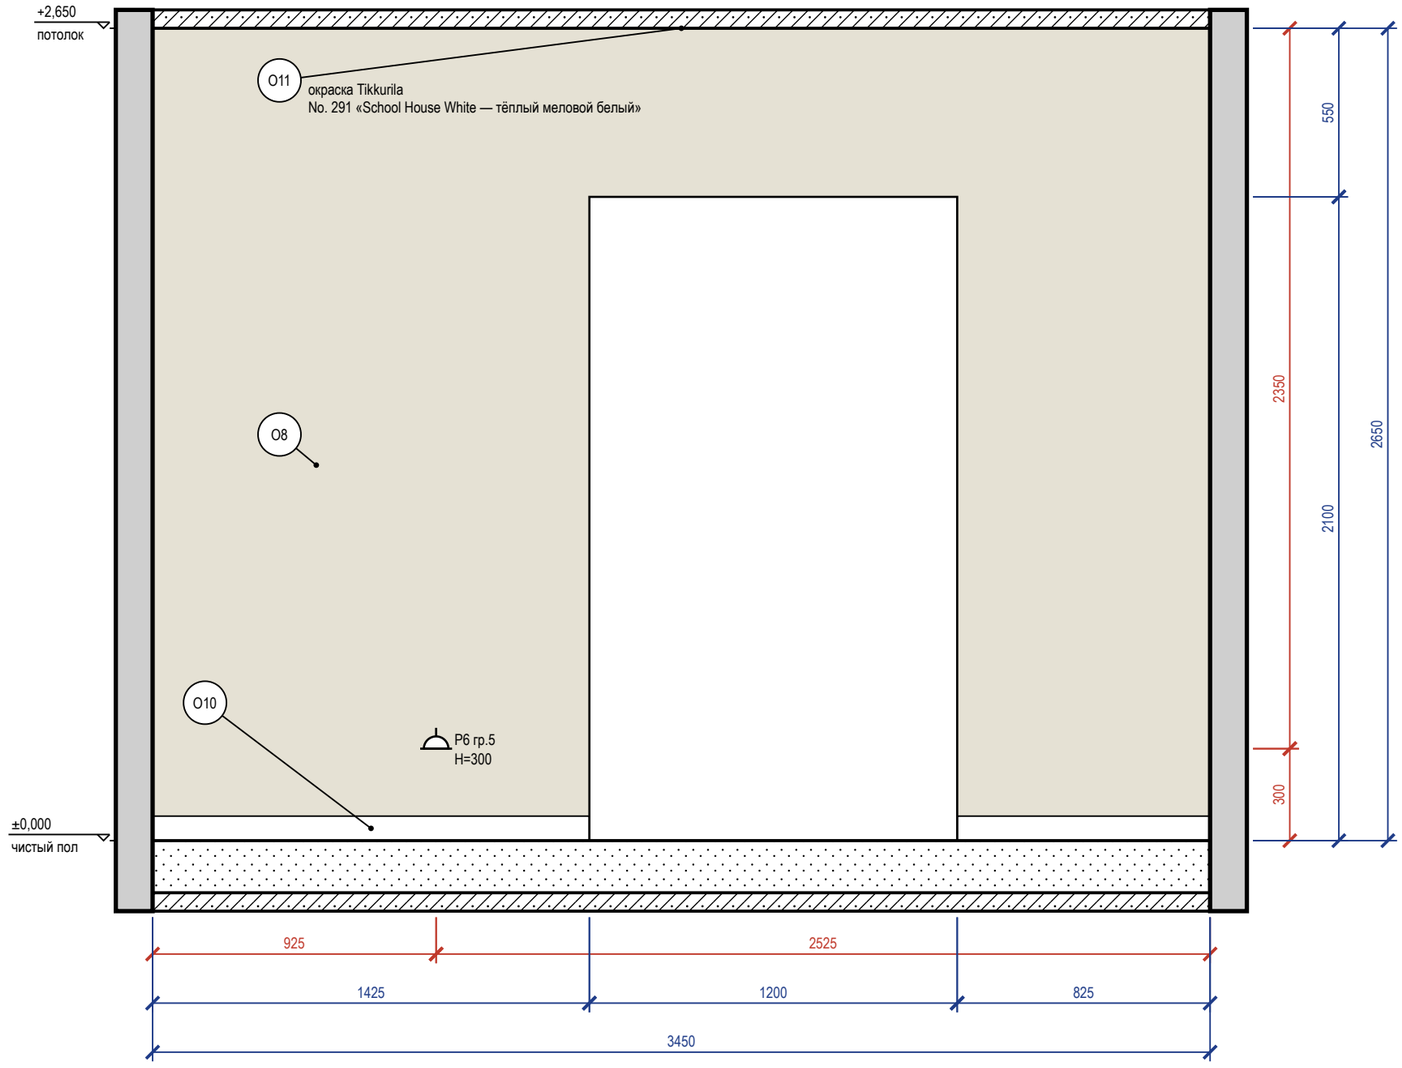


Схема развёрток (М 1:100)

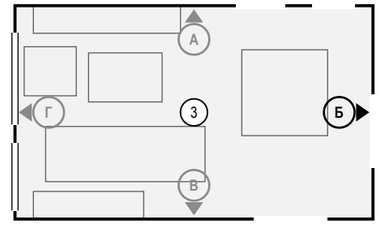

Ведомость отделки (на листе)

Марка	Поверхность	Материал, изделие	Цвет, код	Кол.
О8	стены	окраска, Tikkurila Optiva 5 Matt, матовая, подготовка К3	Farrow & Ball No. 291 «School House White — тёплый меловой белый»	6,6 м²
О10	плинтус	плинтус МДФ, h 80 мм, аналог: плинтус МДФ под окраску 80×16 мм, полуглянцевая	Farrow & Ball No. 291 «School House White — тёплый меловой белый»	2,3 м
О11	потолок	окраска, Tikkurila Anti-Reflex 2, глубокоматовая, подготовка Q3	Farrow & Ball No. 291 «School House White — тёплый меловой белый»	20,3 м²

Визуализация этой стены — лист 43



Примечания

1. Размеры — в мм от чистовых поверхностей стен; условные обозначения и общие указания — лист 2.

					Проект: Квартира 103 м²
	Лист	№ док.	Подпись	Дата	Развёртка стены Б. Гостиная-столовая (пом. 3)
Дизайнер	Кырлан А.С.			18.10.26	

Стадия	Лист	Листов
П	47	103

выпуск 18.10.2026 № d119044df4 · стр. 47 из 103

Развёртка стены В


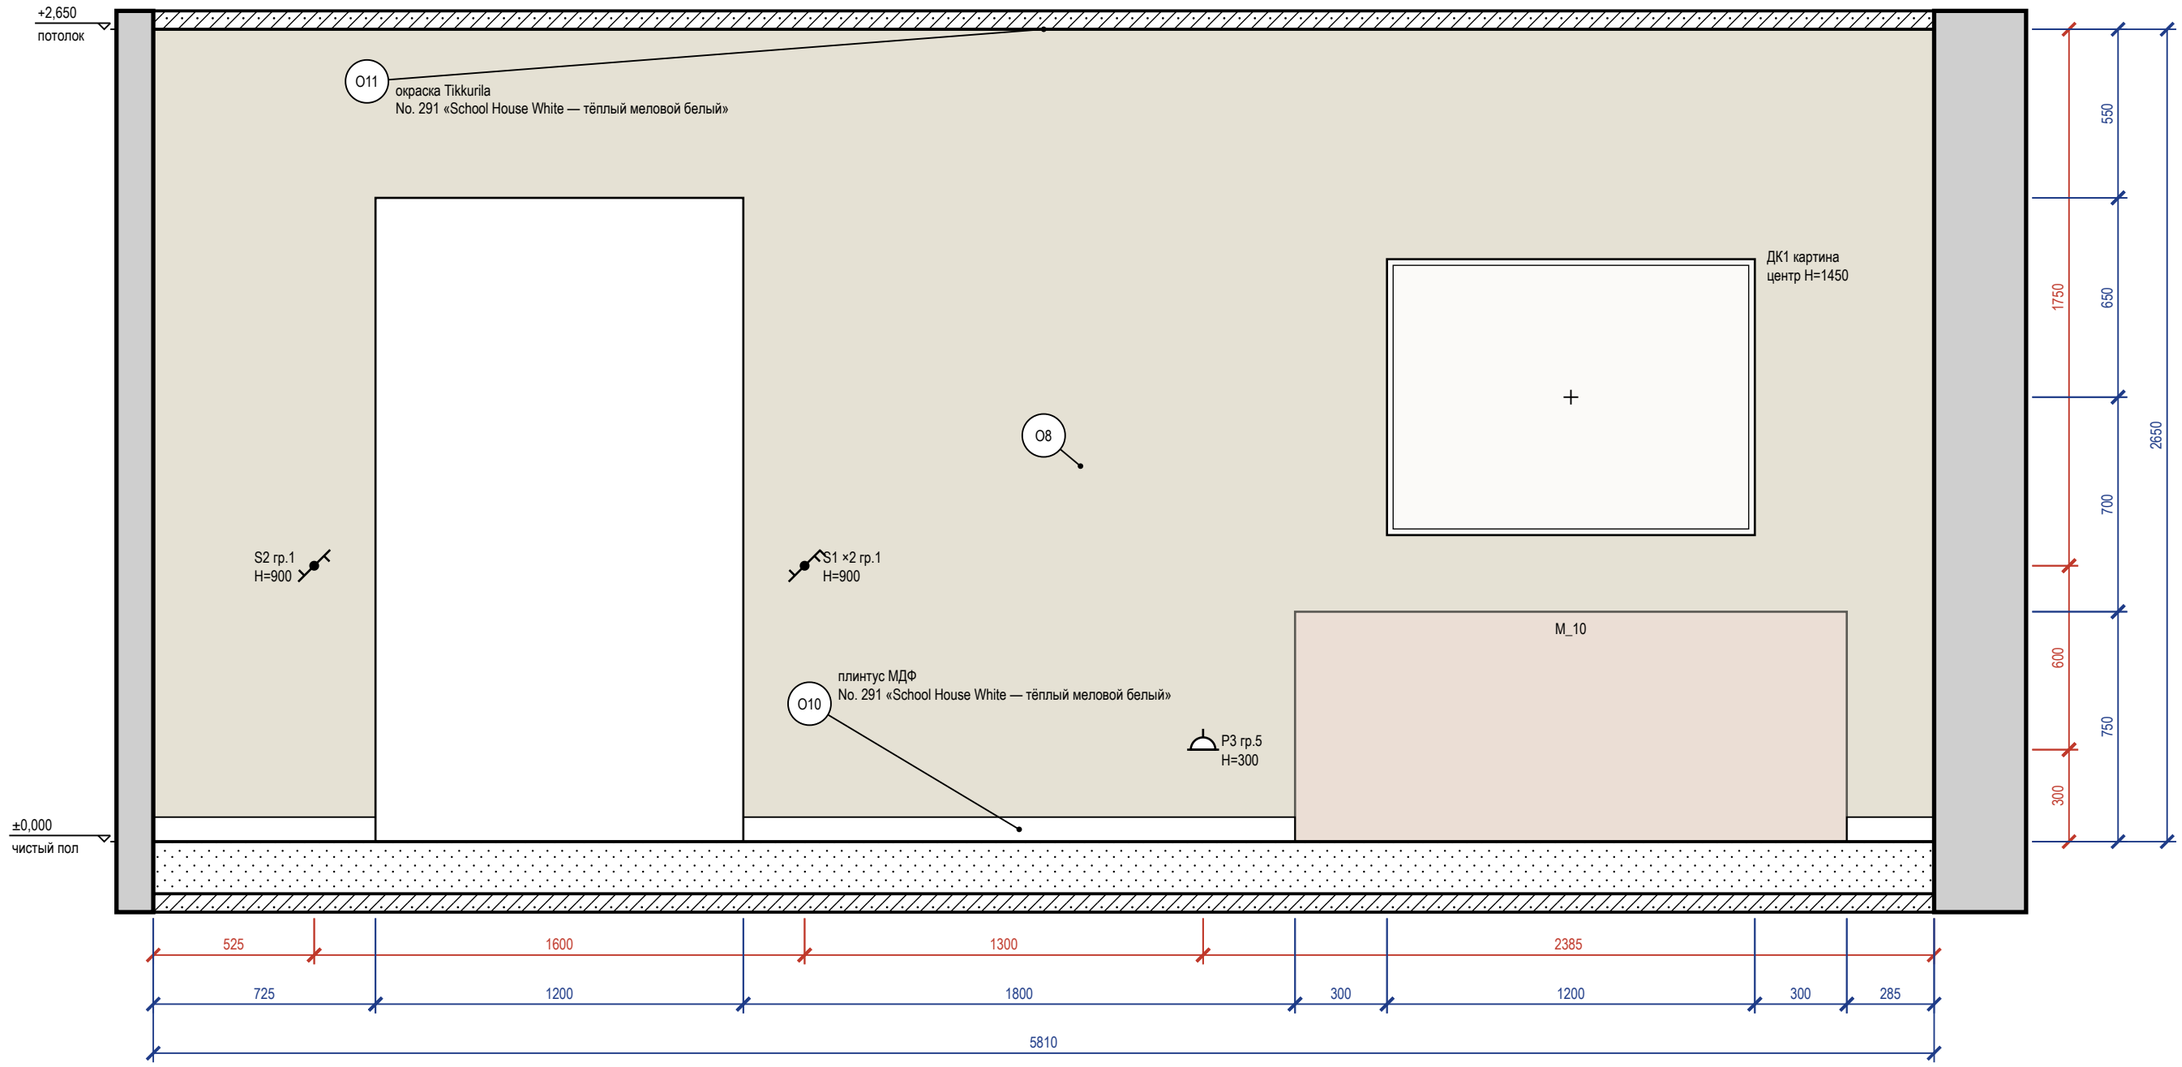



Схема развёрток (М 1:100)

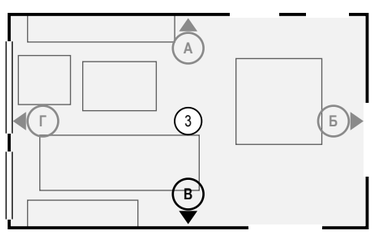

Ведомость отделки (на листе)

Марка	Поверхность	Материал, изделие	Цвет, код	Кол.
О8	стены	окраска, Tikkurila Optiva 5 Matt, матовая, подготовка К3	Farrow & Ball No. 291 «School House White тёплый меловой белый»	12,9 м²
О10	плинтус	плинтус МДФ, h 80 мм, аналог: плинтус МДФ под окраску 80×16 мм, полуглянцевая	Farrow & Ball No. 291 «School House White тёплый меловой белый»	2,8 м
О11	потолок	окраска, Tikkurila Anti-Reflex 2, глубокоматовая, подготовка Q3	Farrow & Ball No. 291 «School House White тёплый меловой белый»	20,3 м²

Визуализация этой стены — лист 44

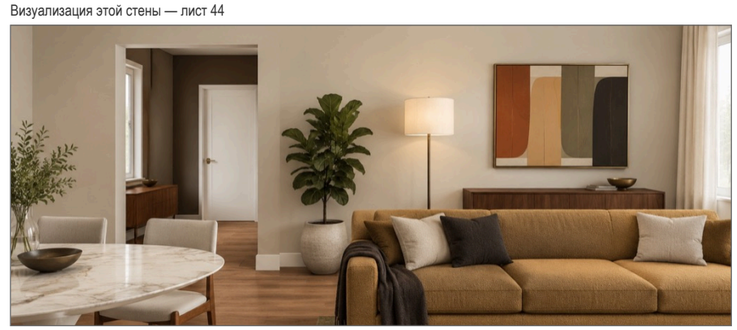

Примечания

1. Размеры — в мм от чистовых поверхностей стен; условные обозначения и общие указания — лист 2.
2. Картины и зеркала крепить к основанию по паспорту изделия (закладные и анкеры — в перечне скрытых работ); крест — ось центра предмета.

					Проект: Квартира 103 м²
	Лист	№ док.	Подпись	Дата	Развёртка стены В. Гостиная-столовая (пом. 3)
Дизайнер	Кырлан А.С.			18.10.26	

Стадия	Лист	Листов
П	48	103

выпуск 18.10.2026 № d119044df4 · стр. 48 из 103

Развёртка стены Г


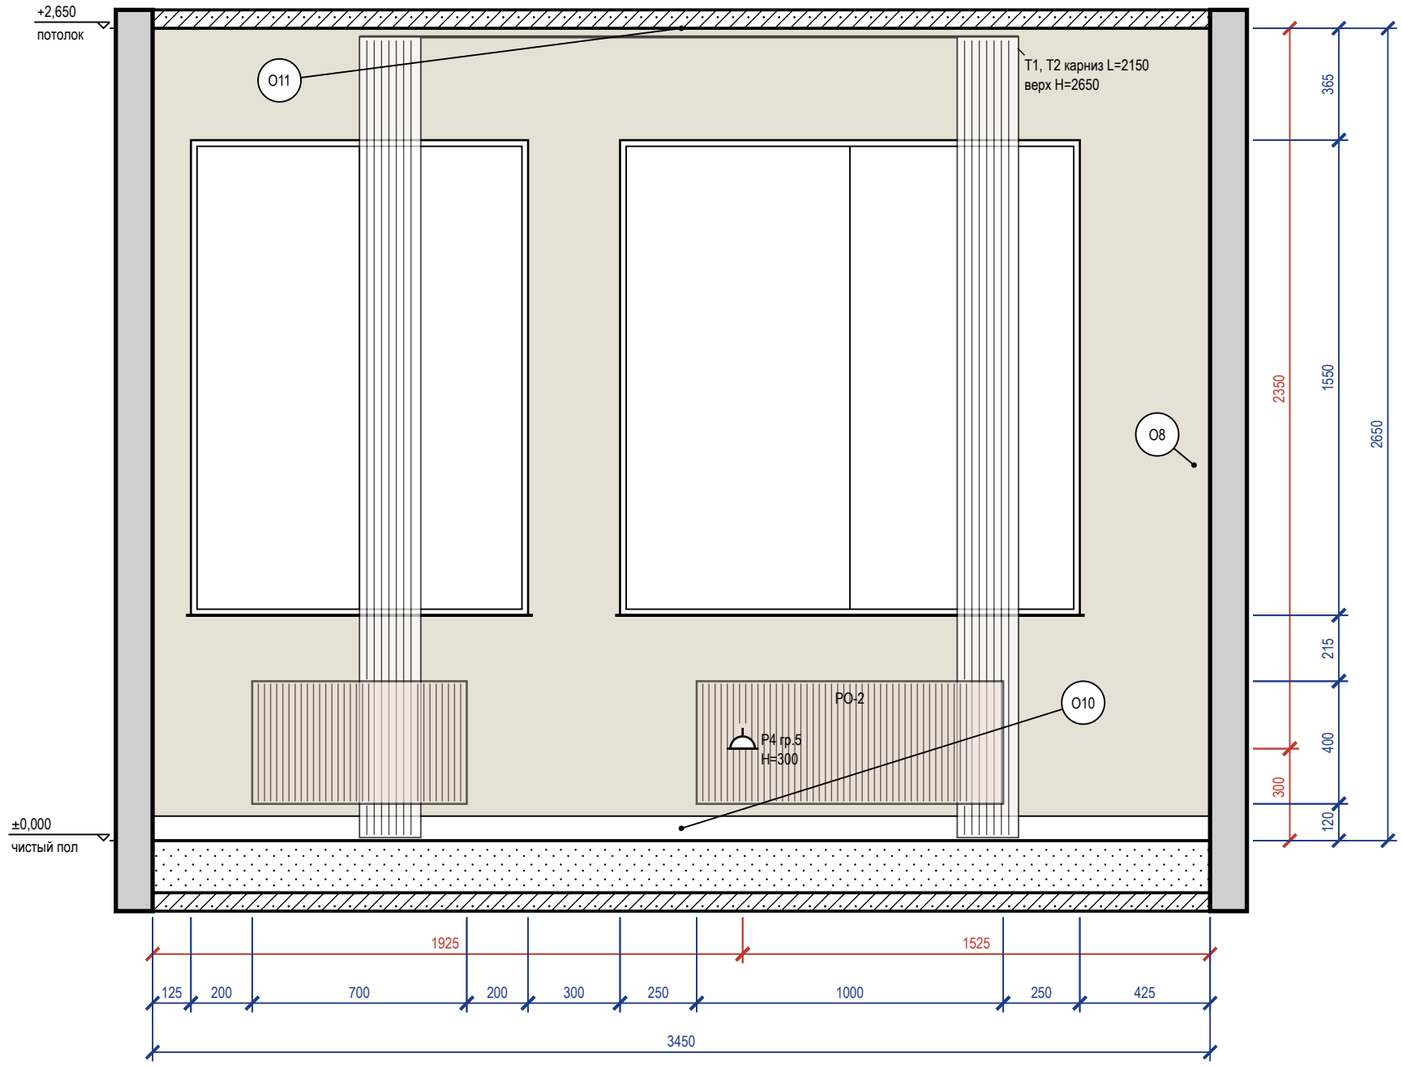


Схема развёрток (М 1:100)

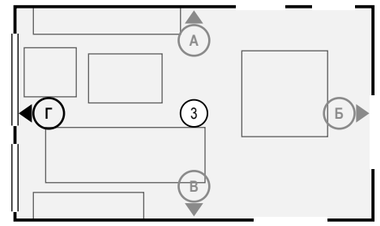

Ведомость отделки (на листе)

Марка	Поверхность	Материал, изделие	Цвет, код	Кол.
О8	стены	окраска, Tikkurila Optiva 5 Matt, матовая, подготовка К3	Farrow & Ball No. 291 «School House White — тёплый меловой белый»	5,1 м²
О10	плинтус	плинтус МДФ, h 80 мм, аналог: плинтус МДФ под окраску 80×16 мм, полуглянцевая	Farrow & Ball No. 291 «School House White — тёплый меловой белый»	3,5 м
О11	потолок	окраска, Tikkurila Anti-Reflex 2, глубокоматовая, подготовка Q3	Farrow & Ball No. 291 «School House White — тёплый меловой белый»	20,3 м²

Визуализация этой стены — лист 45



Примечания

1. Размеры — в мм от чистовых поверхностей стен; условные обозначения и общие указания — лист 2.
2. Карнизы (шины) — по ведомости текстиля декоратора; длина L и верх H — по развёртке, крепление — до окраски потолка.
3. Линии узора (швы плитки, складки штор, рёбра радиаторов) прерываются у знаков и выносок — просвет между линиями не менее 0,7 мм.

					Проект: Квартира 103 м²			
	Лист	№ док.	Подпись	Дата	Развёртка стены Г. Гостиная-столовая (пом. 3)	Стадия	Лист	Листов
Дизайнер	Кырлан А.С.			18.10.26		П	49	103

выпуск 18.10.2026 № d119044df4 · стр. 49 из 103



					Проект: Квартира 103 м²			
	Лист	№ док.	Подпись	Дата				
Дизайнер	Кырлан А.С.			18.10.26	Визуализация: Прихожая-холл	Стадия	Лист	Листов
						П	50	103

выпуск 18.10.2026 № d119044df4 · стр. 50 из 103



					Проект: Квартира 103 м²
	Лист	№ док.	Подпись	Дата	
Дизайнер	Кырлан А.С.			18.10.26	Визуализация: Прихожая-холл

Стадия	Лист	Листов
П	51	103

выпуск 18.10.2026 № d119044df4 · стр. 51 из 103

Развёртка стены А


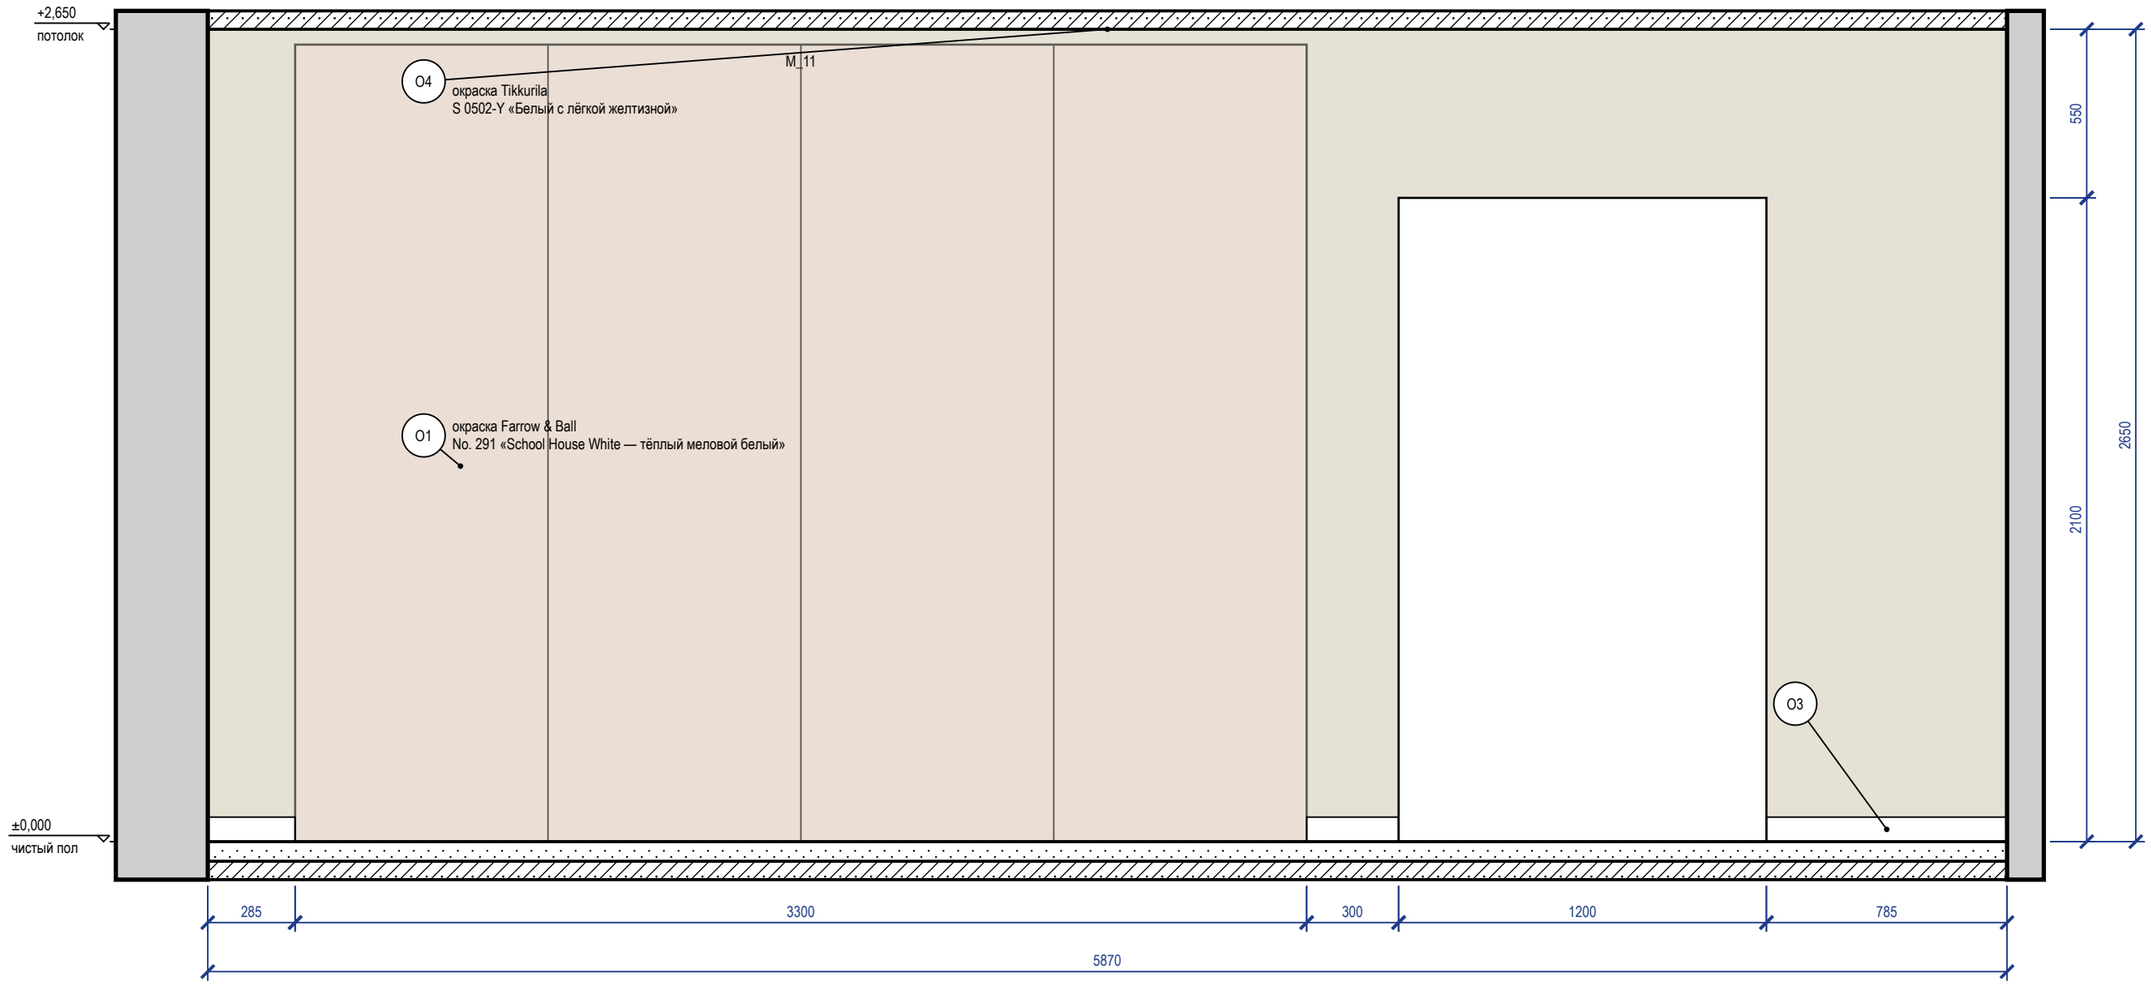


Схема развёрток (М 1:100)

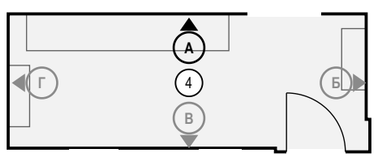

Ведомость отделки (на листе)

Марка	Поверхность	Материал, изделие	Цвет, код	Кол.
О1	стены	окраска, Farrow & Ball Modern Emulsion, матовая, подготовка Q3	Farrow & Ball No. 291 «School House White тёплый меловой белый»	13 м²
О3	плинтус	плинтус МДФ, h 80 мм, аналог: плинтус МДФ под покраску 80×16	Farrow & Ball No. 291 «School House White тёплый меловой белый»	1,4 м
О4	потолок	окраска, Tikkurila Anti-Reflex 2, глубокоматовая, подготовка Q3	NCS S 0502-Y «Белый с лёгкой желтизной»	12,9 м²

Визуализация этой стены — лист 50



Примечания

1. Размеры — в мм от чистовых поверхностей стен; условные обозначения и общие указания — лист 2.

					Проект: Квартира 103 м²
	Лист	№ док.	Подпись	Дата	
Дизайнер	Кырлан А.С.			18.10.26	Развёртка стены А. Прихожая-холл (пом. 4)

Стадия	Лист	Листов
П	52	103

выпуск 18.10.2026 № d119044df4 · стр. 52 из 103

Развёртка стены Б


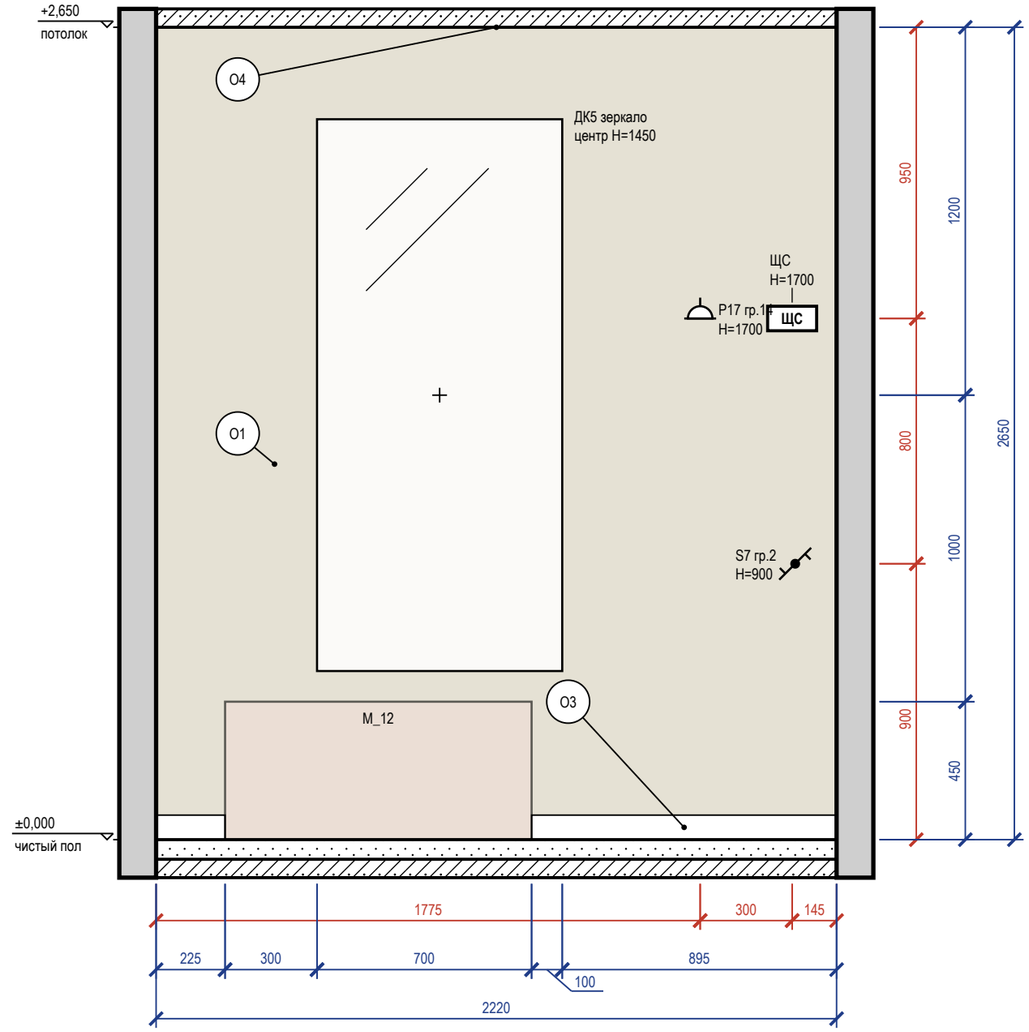


Схема развёрток (М 1:100)

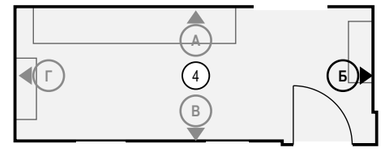

Ведомость отделки (на листе)

Марка	Поверхность	Материал, изделие	Цвет, код	Кол.
О1	стены	окраска, Farrow & Ball Modern Emulsion, матовая, подготовка Q3	Farrow & Ball No. 291 «School House White — тёплый меловой белый»	5,9 м²
О3	плинтус	плинтус МДФ, h 80 мм, аналог: плинтус МДФ под покраску 80×16	Farrow & Ball No. 291 «School House White — тёплый меловой белый»	1,2 м
О4	потолок	окраска, Tikkurila Anti-Reflex 2, глубокоматовая, подготовка Q3	NCS S 0502-Y «Белый с лёгкой желтизной»	12,9 м²

Визуализация этой стены — лист 51



Примечания

1. Размеры — в мм от чистовых поверхностей стен; условные обозначения и общие указания — лист 2.
2. Картины и зеркала крепить к основанию по паспорту изделия (закладные и анкеры — в перечне скрытых работ); крест — ось центра предмета.

					Проект: Квартира 103 м²
	Лист	№ док.	Подпись	Дата	
Дизайнер	Кырлан А.С.			18.10.26	Развёртка стены Б. Прихожая-холл (пом. 4)

Стадия	Лист	Листов
П	53	103

выпуск 18.10.2026 № d119044df4 · стр. 53 из 103

Развёртка стены В


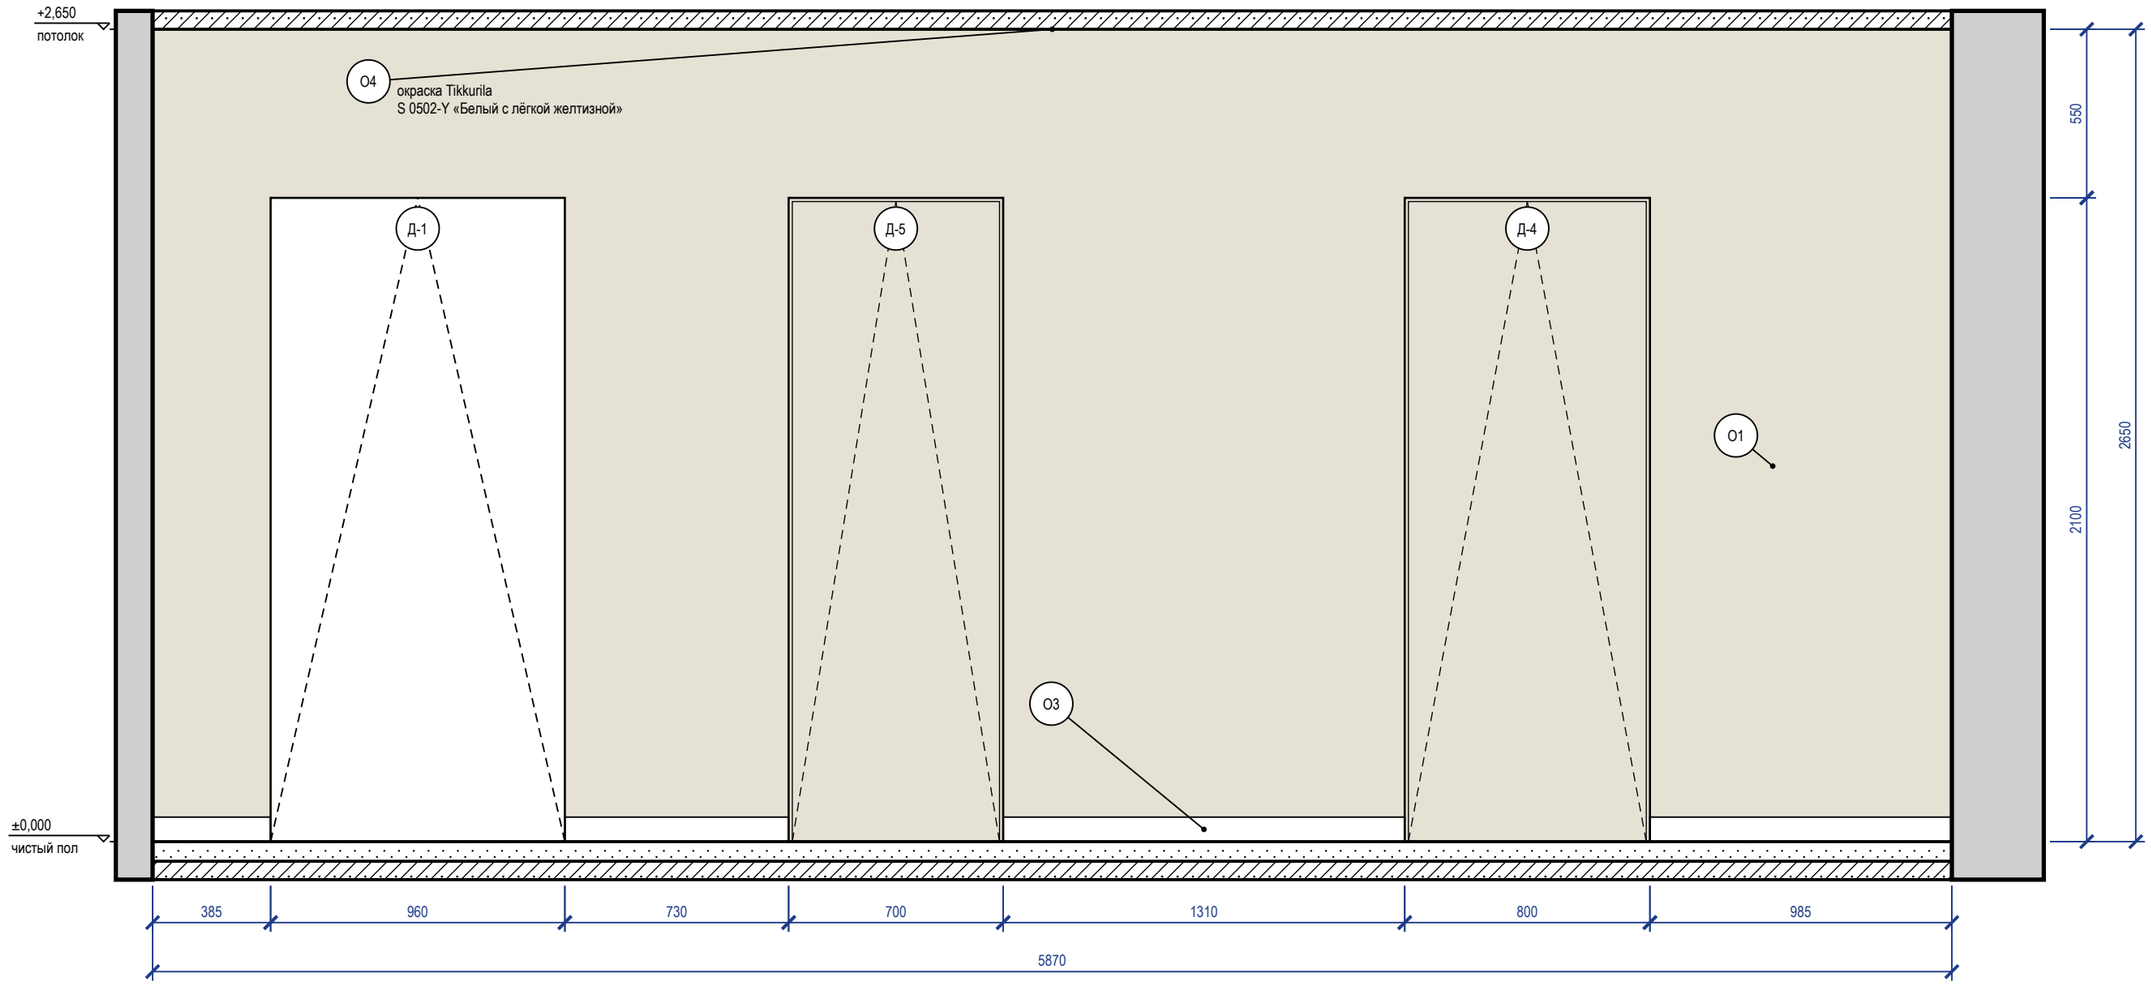


Схема развёрток (М 1:100)

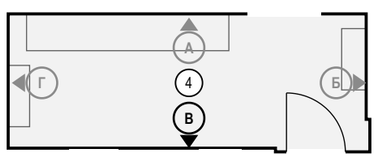

Ведомость отделки (на листе)

Марка	Поверхность	Материал, изделие	Цвет, код	Кол.
О1	стены	окраска, Farrow & Ball Modern Emulsion, матовая, подготовка Q3	Farrow & Ball No. 291 «School House White тёплый меловой белый»	10,4 м²
О3	плинтус	плинтус МДФ, h 80 мм, аналог: плинтус МДФ под покраску 80×16	Farrow & Ball No. 291 «School House White тёплый меловой белый»	3,4 м
О4	потолок	окраска, Tikkurila Anti-Reflex 2, глубокоматовая, подготовка Q3	NCS S 0502-Y «Белый с лёгкой желтизной»	12,9 м²

Примечания

1. Размеры — в мм от чистовых поверхностей стен; условные обозначения и общие указания — лист 2.
2. Двери скрытого монтажа — полотно в плоскости стены, отделка стены по полотну, плинтус прерывается у короба (узел — на листе узлов).

					Проект: Квартира 103 м²
	Лист	№ док.	Подпись	Дата	Развёртка стены В. Прихожая-холл (пом. 4)
Дизайнер	Кырлан А.С.			18.10.26	

Стадия	Лист	Листов
П	54	103

выпуск 18.10.2026 № d119044df4 · стр. 54 из 103

Развёртка стены Г


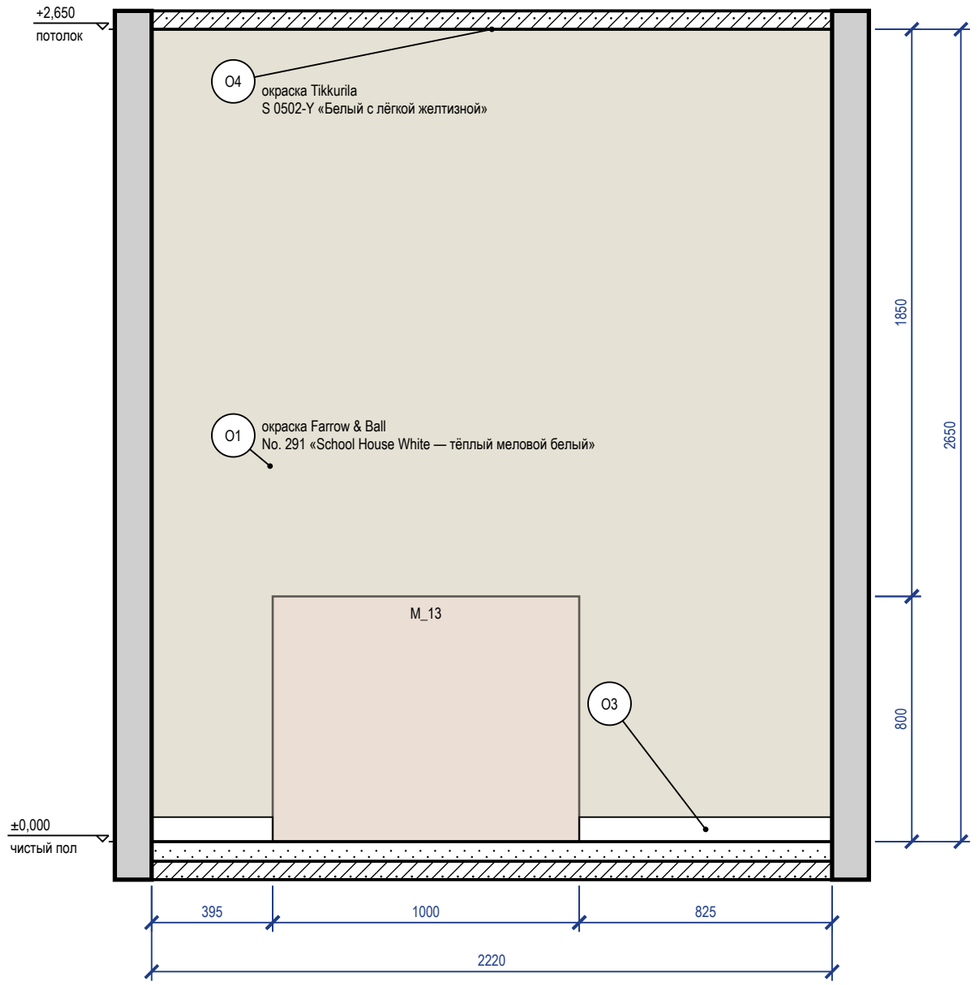


Схема развёрток (М 1:100)

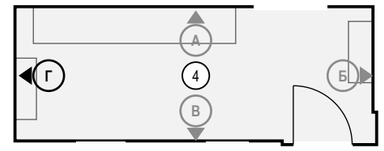

Ведомость отделки (на листе)

Марка	Поверхность	Материал, изделие	Цвет, код	Кол.
О1	стены	окраска, Farrow & Ball Modern Emulsion, матовая, подготовка Q3	Farrow & Ball No. 291 «School House White — тёплый меловой белый»	5,9 м²
О3	плинтус	плинтус МДФ, h 80 мм, аналог: плинтус МДФ под покраску 80×16	Farrow & Ball No. 291 «School House White — тёплый меловой белый»	1,2 м
О4	потолок	окраска, Tikkurila Anti-Reflex 2, глубокоматовая, подготовка Q3	NCS S 0502-Y «Белый с лёгкой желтизной»	12,9 м²

Примечания

1. Размеры — в мм от чистовых поверхностей стен; условные обозначения и общие указания — лист 2.

					Проект: Квартира 103 м²
	Лист	№ док.	Подпись	Дата	Развёртка стены Г. Прихожая-холл (пом. 4)
Дизайнер	Кырлан А.С.			18.10.26	

Стадия	Лист	Листов
П	55	103

выпуск 18.10.2026 № d119044df4 · стр. 55 из 103



					Проект: Квартира 103 м²
	Лист	№ док.	Подпись	Дата	Визуализация кухни
Дизайнер	Кырлан А.С.			18.10.26	

Стадия	Лист	Листов
П	56	103

выпуск 18.10.2026 № d119044df4 · стр. 56 из 103



					Проект: Квартира 103 м²
	Лист	№ док.	Подпись	Дата	
Дизайнер	Кырлан А.С.			18.10.26	Визуализация кухни

Стадия	Лист	Листов
П	57	103

выпуск 18.10.2026 № d119044df4 · стр. 57 из 103

Развёртка стены А


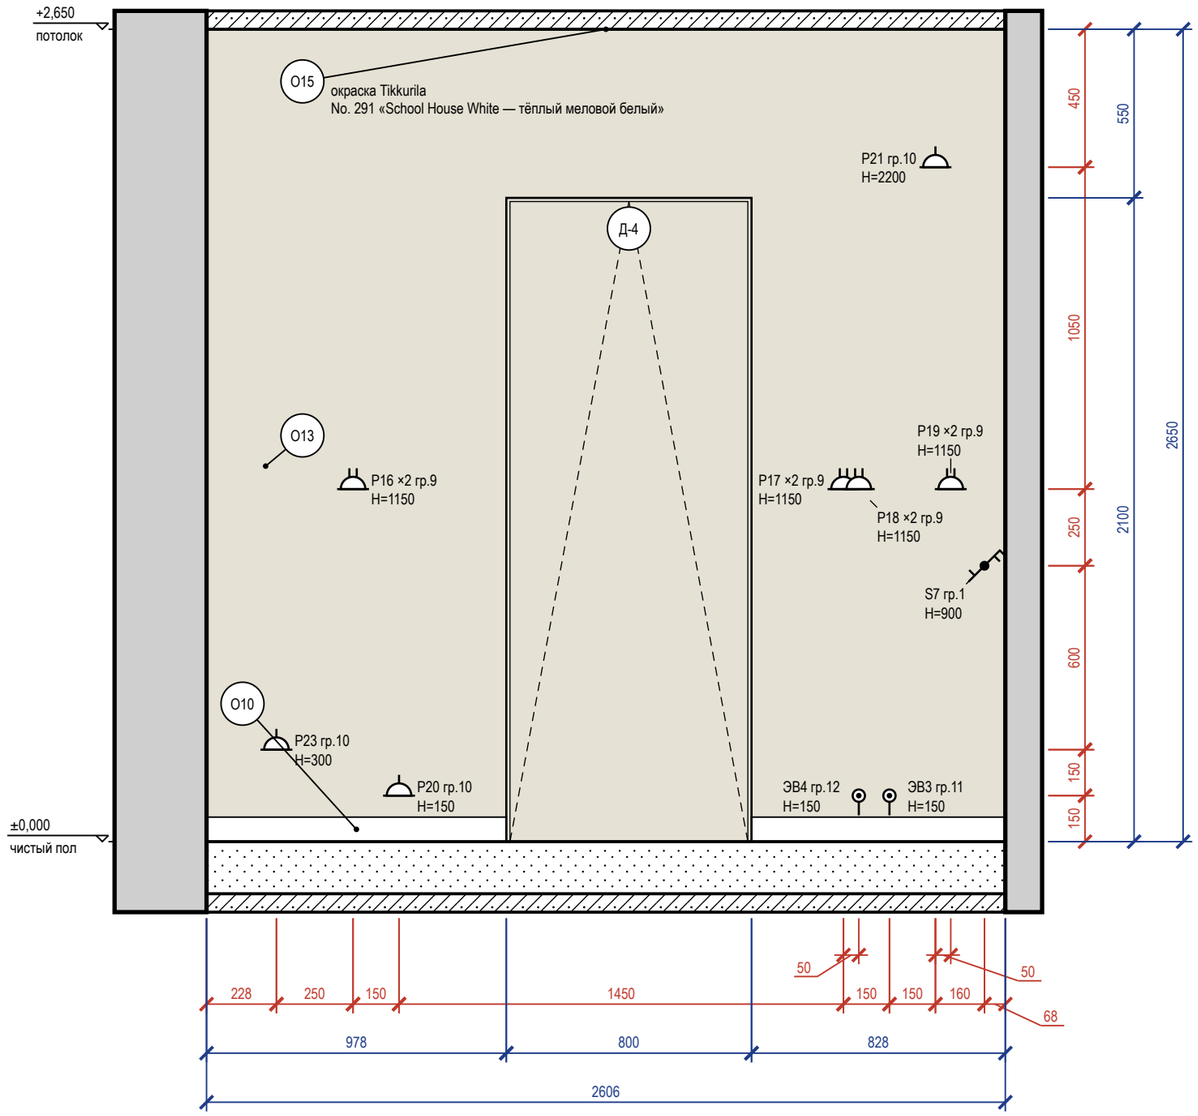


Схема развёрток (М 1:100)

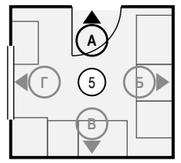

Ведомость отделки (на листе)

Марка	Поверхность	Материал, изделие	Цвет, код	Кол.
О10	плинтус	плинтус МДФ, h 80 мм, аналог: плинтус МДФ под окраску 80×16 мм, полуглянцевая	Farrow & Ball No. 291 «School House White — тёплый меловой белый»	1,8 м
О13	стены	окраска, Tikkurila Luja 7, шелковисто-матовая, подготовка К3	Farrow & Ball No. 291 «School House White — тёплый меловой белый»	5,2 м²
О15	потолок	окраска, Tikkurila Luja 7, матовая, подготовка Q3	Farrow & Ball No. 291 «School House White — тёплый меловой белый»	6,5 м²

Примечания

1. Размеры — в мм от чистовых поверхностей стен; условные обозначения и общие указания — лист 2.
2. Двери скрытого монтажа — полотно в плоскости стены, отделка стены по полотну, плинтус прерывается у короба (узел — на листе узлов).
3. Выводы кухонной техники — по утверждённому проекту кухни: привязки выводов даются от осей модулей гарнитура.

					Проект: Квартира 103 м²
	Лист	№ док.	Подпись	Дата	Развёртка стены А. Кухня (пом. 5), кухонный фронт
Дизайнер	Кырлан А.С.			18.10.26	

Стадия	Лист	Листов
П	58	103

выпуск 18.10.2026 № d119044df4 · стр. 58 из 103

Развёртка стены Б


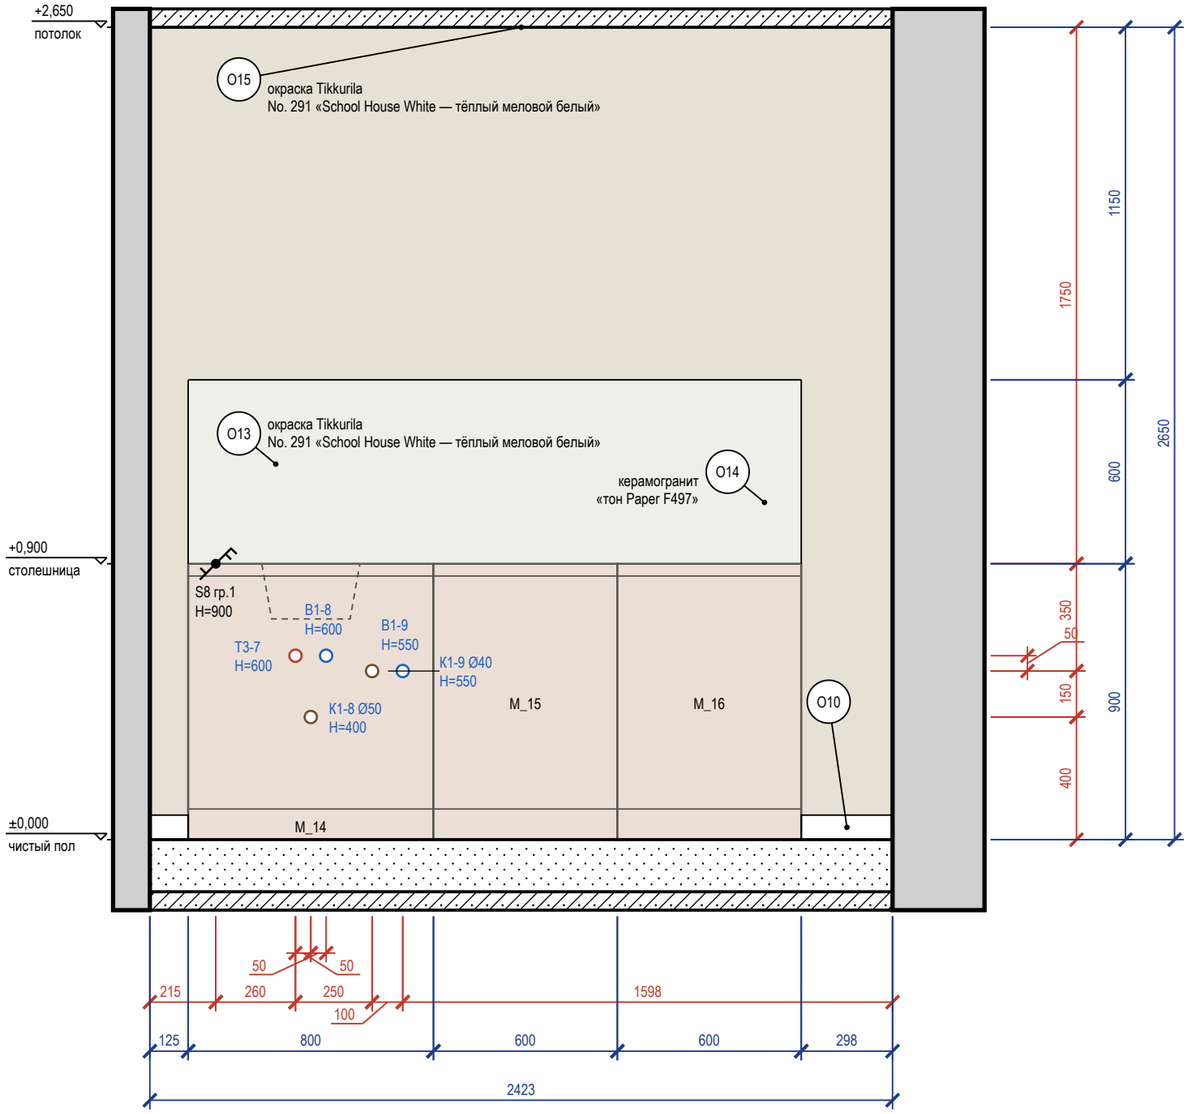


Схема развёрток (М 1:100)

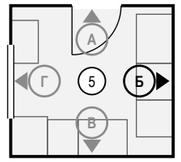

Ведомость отделки (на листе)

Марка	Поверхность	Материал, изделие	Цвет, код	Кол.
О10	плинтус	плинтус МДФ, h 80 мм, аналог: плинтус МДФ под окраску 80×16 мм, полуглянцевая	Farrow & Ball No. 291 «School House White — тёплый меловой белый»	0,4 м
О13	стены	окраска, Tikkurila Luja 7, шелковисто-матовая, подготовка К3	Farrow & Ball No. 291 «School House White — тёплый меловой белый»	5,2 м²
О14	фартук	керамогранит, аналог: керамогранит матовый, тон F497, затирка CG2WA	#F1F1EC «тон Paper F497»	1,2 м²
О15	потолок	окраска, Tikkurila Luja 7, матовая, подготовка Q3	Farrow & Ball No. 291 «School House White — тёплый меловой белый»	6,5 м²

Визуализация этой стены — лист 56



Примечания

1. Размеры — в мм от чистовых поверхностей стен; условные обозначения и общие указания — лист 2.
2. Выводы ВК — коды и высоты по листу выводов сантехники.
3. Выводы кухонной техники — по утверждённому проекту кухни: привязки выводов даются от осей модулей гарнитура.

					Проект: Квартира 103 м²
	Лист	№ док.	Подпись	Дата	
Дизайнер	Кырлан А.С.			18.10.26	Развёртка стены Б. Кухня (пом. 5), кухонный фронт

Стадия	Лист	Листов
П	59	103

выпуск 18.10.2026 № d119044df4 · стр. 59 из 103

Развёртка стены В


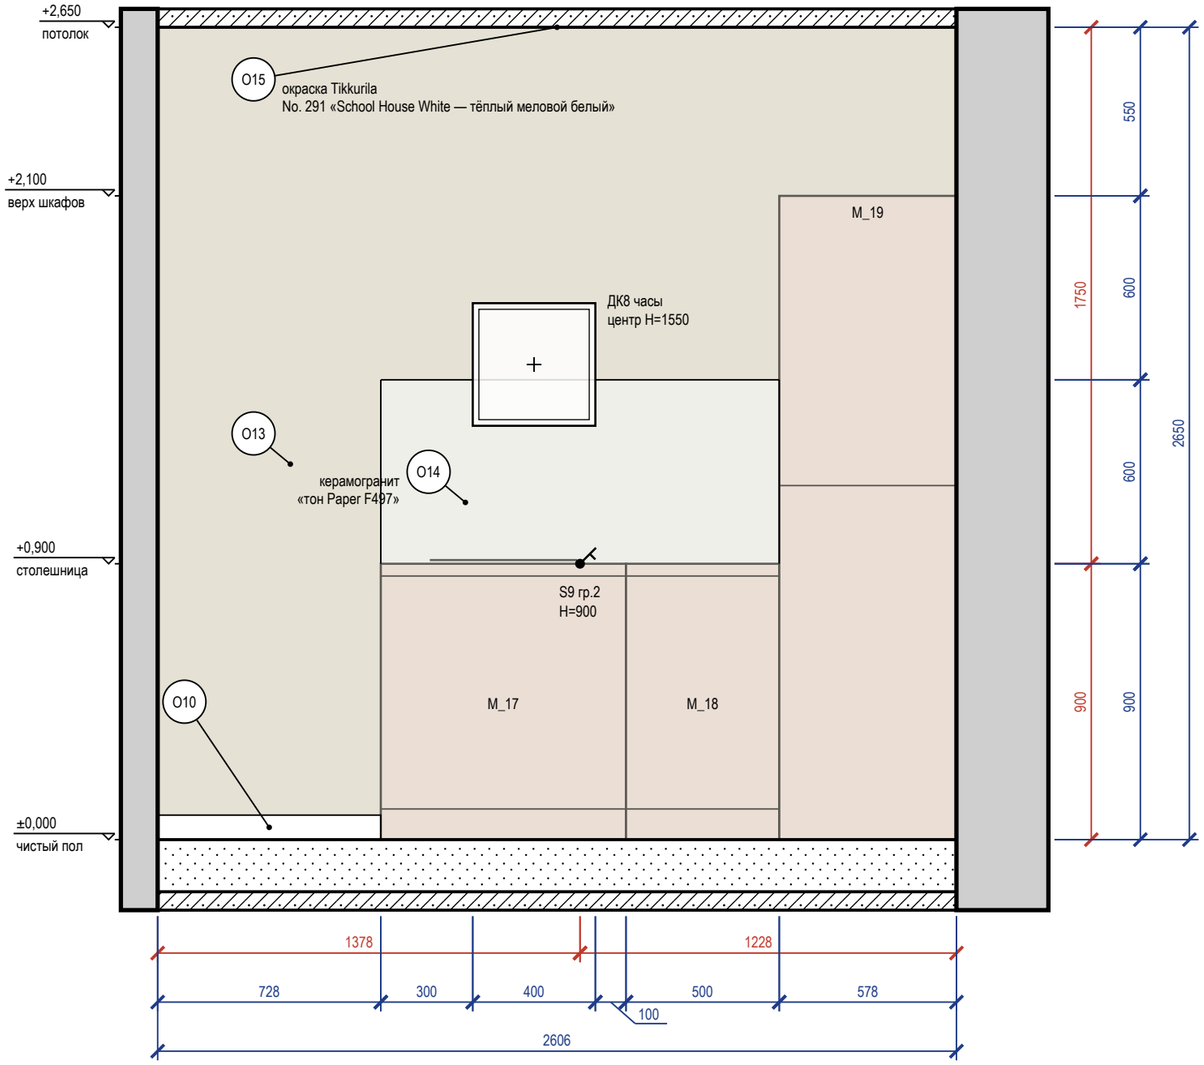


Схема развёрток (М 1:100)

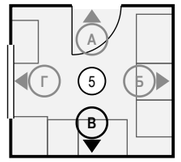

Ведомость отделки (на листе)

Марка	Поверхность	Материал, изделие	Цвет, код	Кол.
О10	плинтус	плинтус МДФ, h 80 мм, аналог: плинтус МДФ под окраску 80×16 мм, полуглянцевая	Farrow & Ball No. 291 «School House White — тёплый меловой белый»	0,7 м
О13	стены	окраска, Tikkurila Luja 7, шелковисто-матовая, подготовка К3	Farrow & Ball No. 291 «School House White — тёплый меловой белый»	6,1 м²
О14	фартук	керамогранит, аналог: керамогранит матовый, тон F497, затирка CG2WA	#F1F1EC «тон Paper F497»	0,8 м²
О15	потолок	окраска, Tikkurila Luja 7, матовая, подготовка Q3	Farrow & Ball No. 291 «School House White — тёплый меловой белый»	6,5 м²

Визуализация этой стены — лист 57



Примечания

1. Размеры — в мм от чистовых поверхностей стен; условные обозначения и общие указания — лист 2.
2. Картины и зеркала крепить к основанию по паспорту изделия (закладные и анкеры — в перечне скрытых работ); крест — ось центра предмета.
3. Выводы кухонной техники — по утверждённому проекту кухни: привязки выводов даются от осей модулей гарнитура.

	Лист	№ док.	Подпись	Дата
Дизайнер	Кырлан А.С.			18.10.26

Проект: Квартира 103 м²

Развёртка стены В. Кухня (пом. 5), кухонный фронт

Стадия	Лист	Листов
П	60	103

выпуск 18.10.2026 № d119044df4 · стр. 60 из 103

Развёртка стены Г


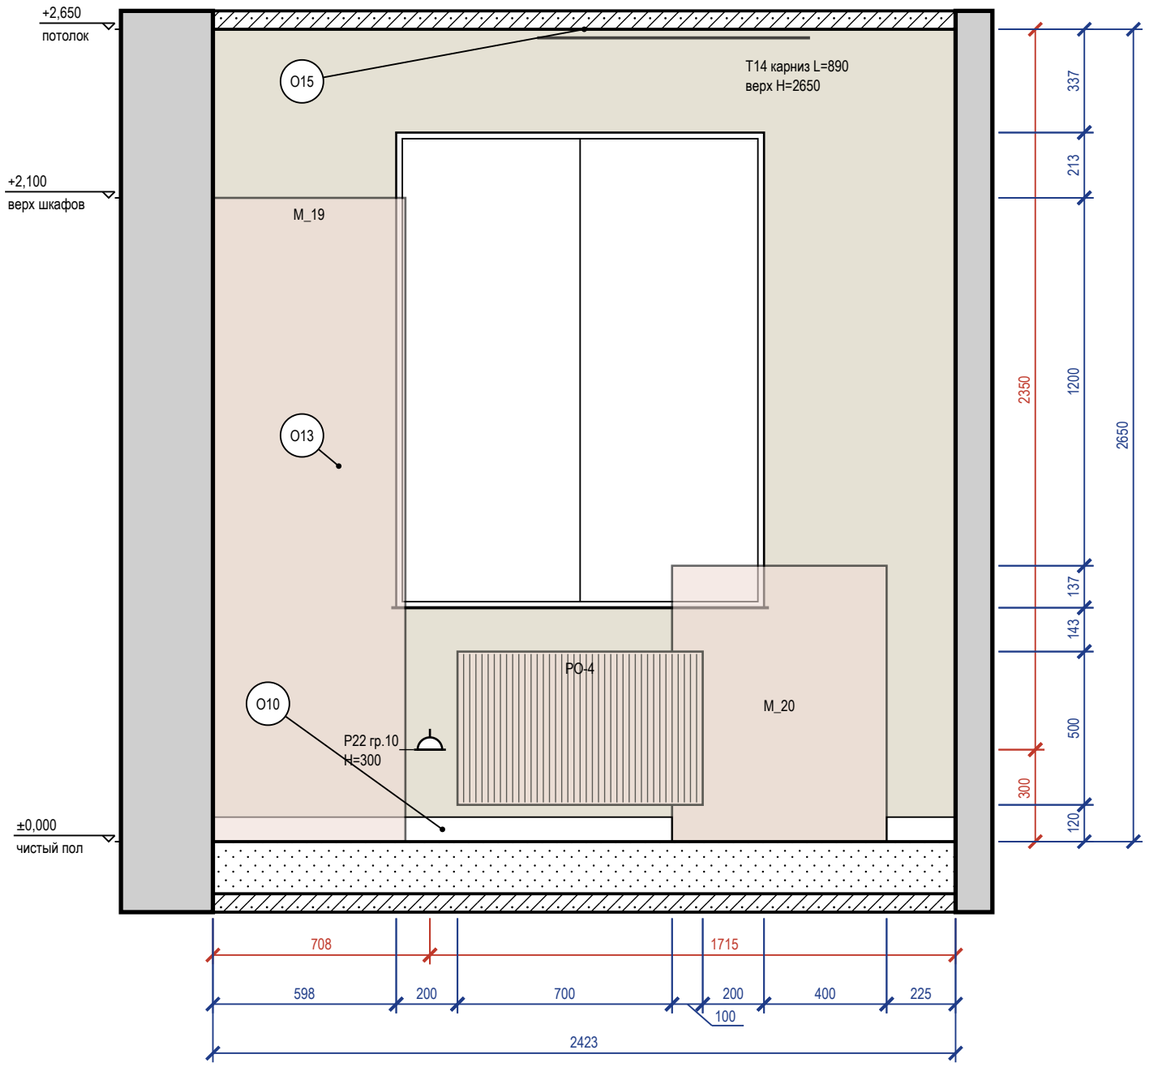


Схема развёрток (М 1:100)

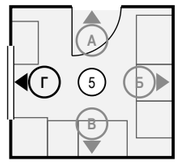

Ведомость отделки (на листе)

Марка	Поверхность	Материал, изделие	Цвет, код	Кол.
О10	плинтус	плинтус МДФ, h 80 мм, аналог: плинтус МДФ под окраску 80×16 мм, полуглянцевая	Farrow & Ball No. 291 «School House White — тёплый меловой белый»	1,7 м
О13	стены	окраска, Tikkurila Luja 7, шелковисто-матовая, подготовка К3	Farrow & Ball No. 291 «School House White — тёплый меловой белый»	4,6 м²
О15	потолок	окраска, Tikkurila Luja 7, матовая, подготовка Q3	Farrow & Ball No. 291 «School House White — тёплый меловой белый»	6,5 м²

Примечания

1. Размеры — в мм от чистовых поверхностей стен; условные обозначения и общие указания — лист 2.
2. Карнизы (шины) — по ведомости текстиля декоратора; длина L и верх H — по развёртке, крепление — до окраски потолка.

					Проект: Квартира 103 м²
	Лист	№ док.	Подпись	Дата	
Дизайнер	Кырлан А.С.			18.10.26	Развёртка стены Г. Кухня (пом. 5)
					Стадия: П; Лист: 61; Листов: 103

выпуск 18.10.2026 № d119044df4 · стр. 61 из 103



					Проект: Квартира 103 м²	
	Лист	№ док.	Подпись	Дата	Визуализация ванной	Стадия / Лист / Листов
Дизайнер	Кырлан А.С.			18.10.26		П / 62 / 103

выпуск 18.10.2026 № d1190444df4 · стр. 62 из 103



					Проект: Квартира 103 м²
	Лист	№ док.	Подпись	Дата	Визуализация ванной
Дизайнер	Кырлан А.С.			18.10.26	

Стадия	Лист	Листов
П	63	103

выпуск 18.10.2026 № d119044df4 · стр. 63 из 103




					Проект: Квартира 103 м²
	Лист	№ док.	Подпись	Дата	
Дизайнер	Кырлан А.С.			18.10.26	Визуализация ванной

Стадия	Лист	Листов
П	64	103

выпуск 18.10.2026 № d119044df4 · стр. 64 из 103

Развёртка стены А

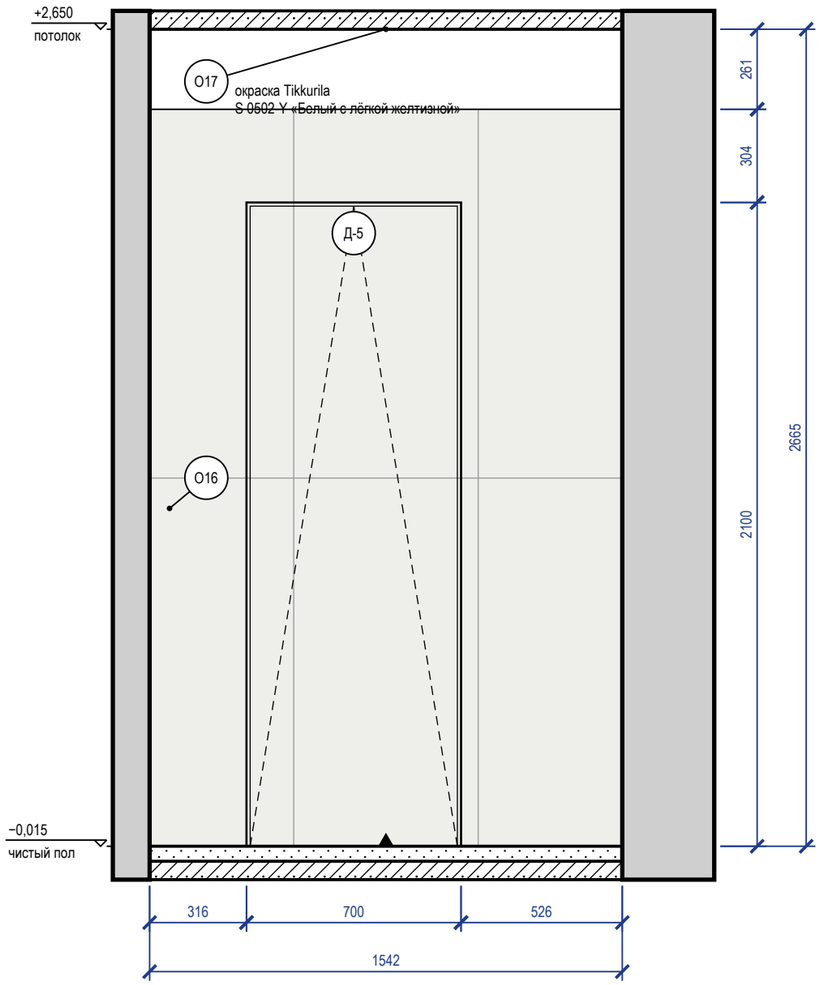

Развёртка стены Б


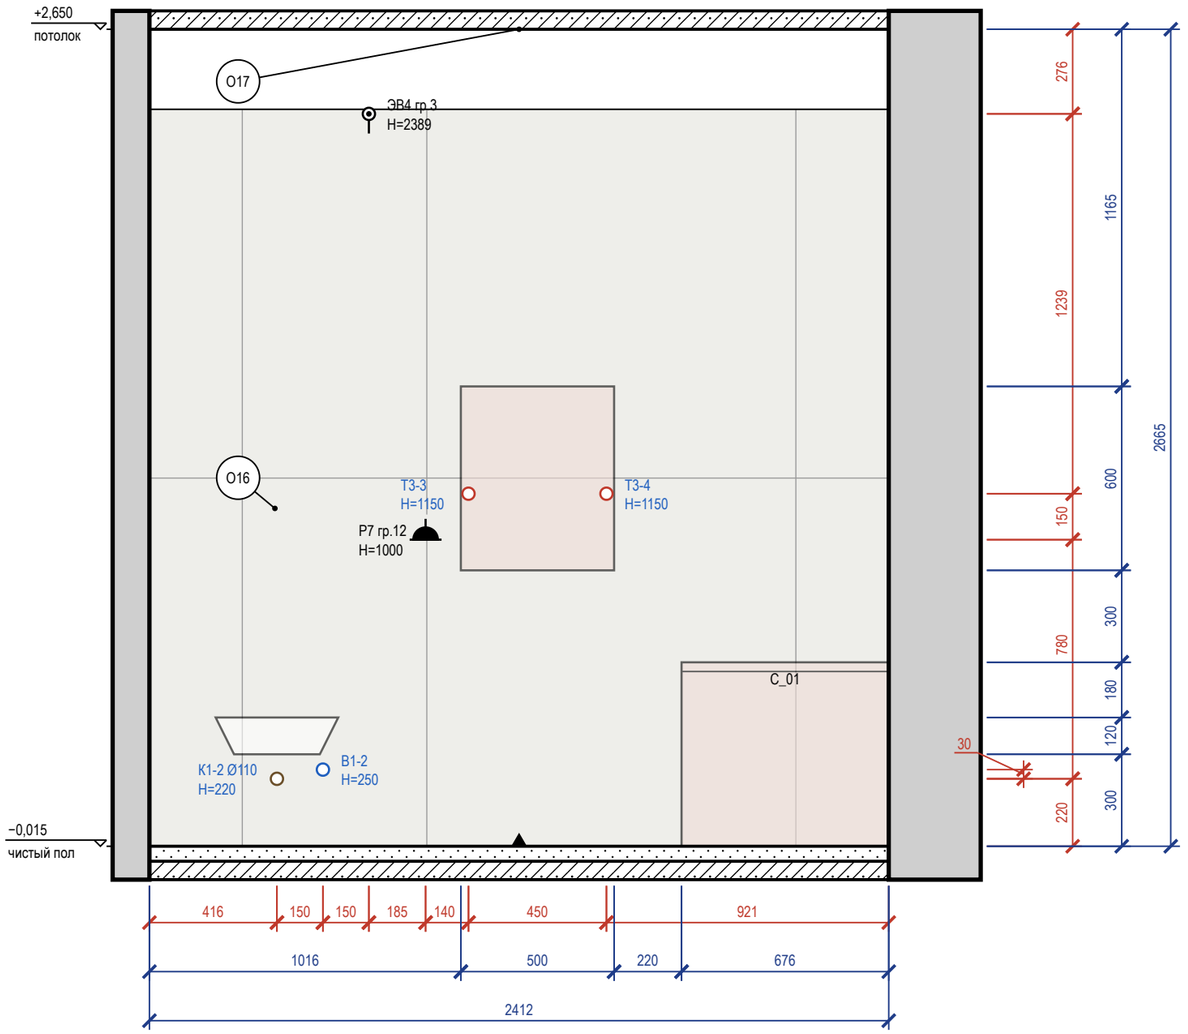



Схема развёрток (М 1:100)

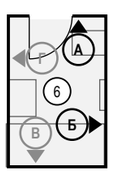

Ведомость отделки (на листе)

Марка	Поверхность	Материал, изделие	Цвет, код	Кол.
О16	стены	облицовка плиткой, Atlas Concorde Marvel Travertine, 600×1200×9 мм, A8UZ, затирка CG2WA	Atlas Concorde A8UZ «Marvel Travertine»	8 м²
О17	потолок	окраска, Tikkurila Luja 7, матовая, подготовка Q3	NCS S 0502-Y «Белый с лёгкой желтизной»	3,9 м²

Визуализация этой стены — лист 62

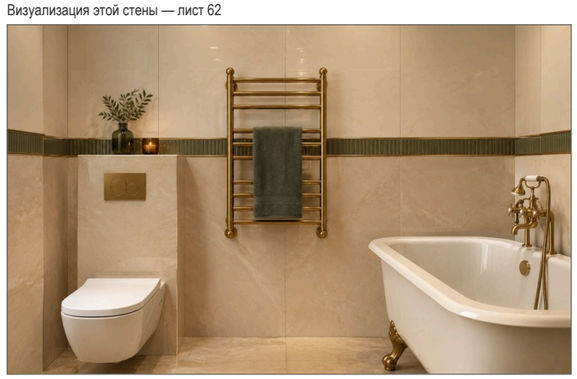

Примечания


1. Размеры — в мм от чистовых поверхностей стен; условные обозначения и общие указания — лист 2.
2. Схема мебели, приборов и декора не является технической документацией для производства мебели; габариты — по паспортам изделий.
3. Выводы ВК — коды и высоты по листу выводов сантехники.
4. Облицовка — по сетке швов 2 мм, раскладка от оси стены (треугольник у пола), целые ряды от пола; подрезки — по листу раскладки плитки.
5. Гидроизоляция в 2 слоя, заход на стены 200 мм — до облицовки, с актом скрытых работ и тестом проливом (узел — на листе узлов).
6. Двери скрытого монтажа — полотно в плоскости стены, отделка стены по полотну, плинтус прерывается у короба (узел — на листе узлов).
7. Линии узора (швы плитки, складки штор, рёбра радиаторов) прерываются у знаков и выносок — просвет между линиями не менее 0,7 мм.

					Проект: Квартира 103 м²
	Лист	№ док.	Подпись	Дата	Развёртки стен А, Б. Ванная (пом. 6)
Дизайнер	Кырлан А.С.			18.10.26	

Стадия	Лист	Листов
П	65	103

выпуск 18.10.2026 № d119044df4 · стр. 65 из 103

Развёртка стены В

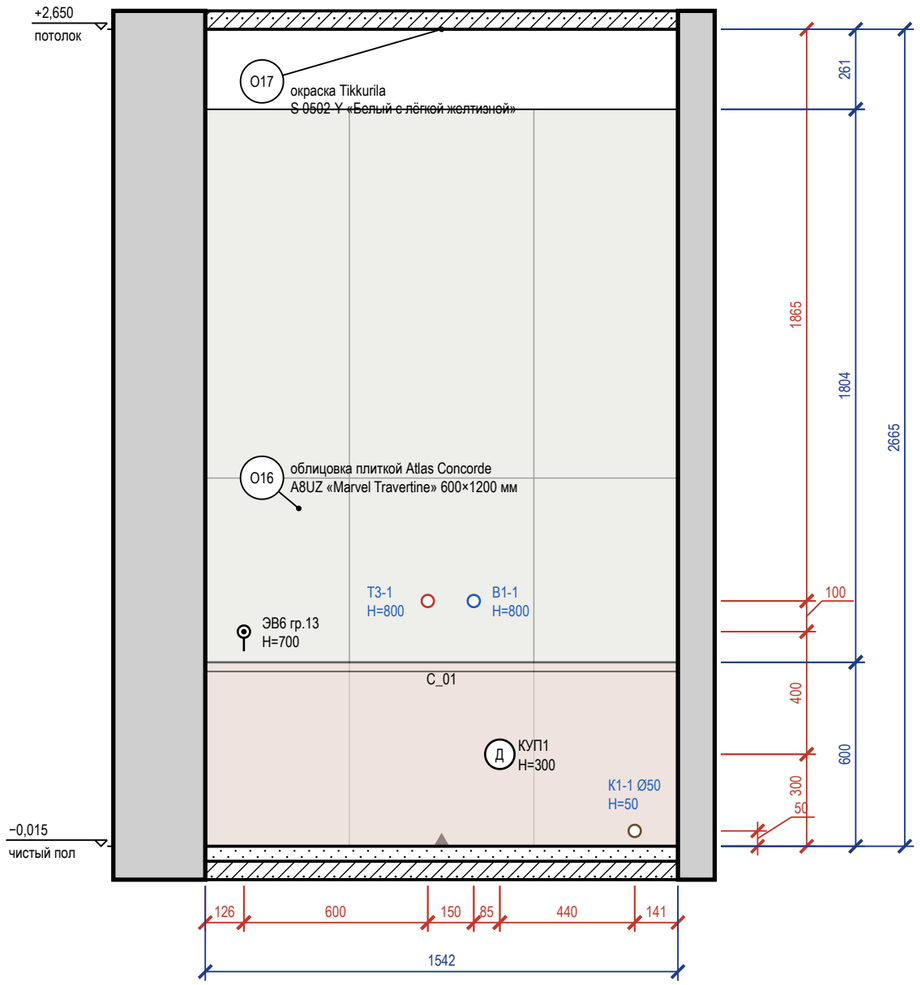

Развёртка стены Г


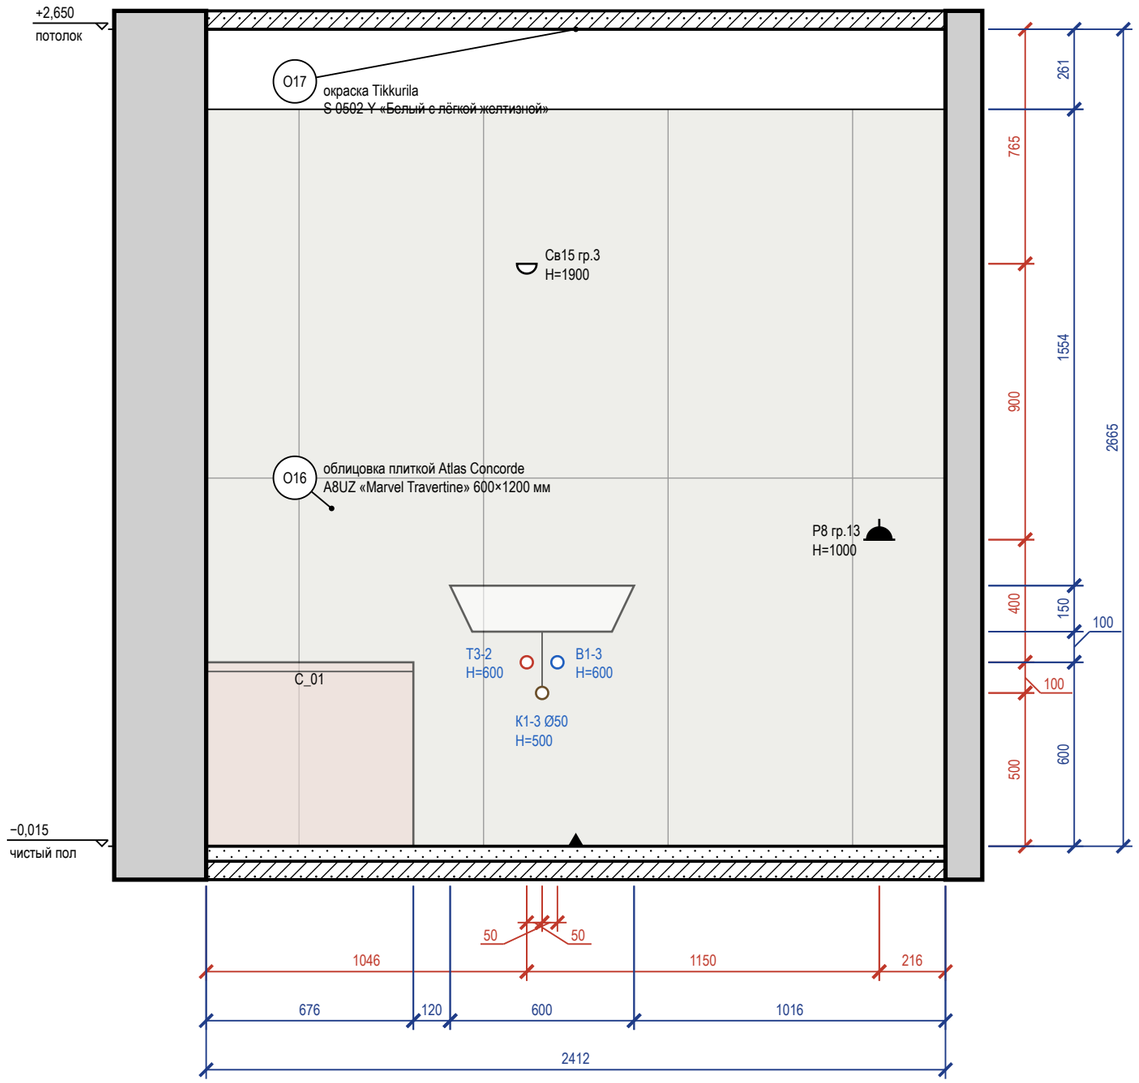


Схема развёрток (М 1:100)

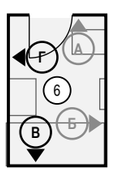

Ведомость отделки (на листе)

Марка	Поверхность	Материал, изделие	Цвет, код	Кол.
О16	стены	облицовка плиткой, Atlas Concorde Marvel Travertine, 600×1200×9 мм, A8UZ, затирка CG2WA	Atlas Concorde A8UZ «Marvel Travertine»	9,5 м²
О17	потолок	окраска, Tikkurila Luja 7, матовая, подготовка Q3	NCS S 0502-Y «Белый с лёгкой желтизной»	3,9 м²

Визуализация этой стены — лист 63



Примечания

1. Размеры — в мм от чистовых поверхностей стен; условные обозначения и общие указания — лист 2.
2. Схема мебели, приборов и декора не является технической документацией для производства мебели; габариты — по паспортам изделий.
3. Выводы ВК — коды и высоты по листу выводов сантехники.
4. Облицовка — по сетке швов 2 мм, раскладка от оси стены (треугольник у пола), целые ряды от пола; подрезки — по листу раскладки плитки.
5. Гидроизоляция в 2 слоя, заход на стены 200 мм — до облицовки, с актом скрытых работ и тестом проливом (узел — на листе узлов).

					Проект: Квартира 103 м²
	Лист	№ док.	Подпись	Дата	Развёртки стен В, Г. Ванная (пом. 6)
Дизайнер	Кырлан А.С.			18.10.26	

Стадия	Лист	Листов
П	66	103

выпуск 18.10.2026 № d119044df4 · стр. 66 из 103




					Проект: Квартира 103 м²
	Лист	№ док.	Подпись	Дата	
Дизайнер	Кырлан А.С.			18.10.26	Визуализация постирочной


Стадия	Лист	Листов
П	67	103

выпуск 18.10.2026 № d119044df4 · стр. 67 из 103

Развёртка стены А

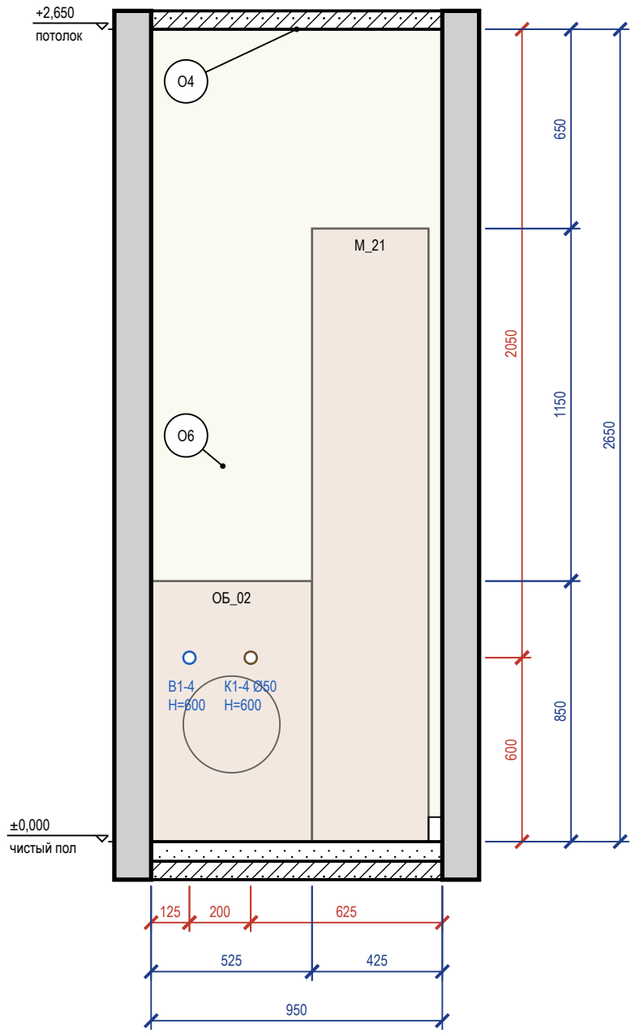

Развёртка стены Б

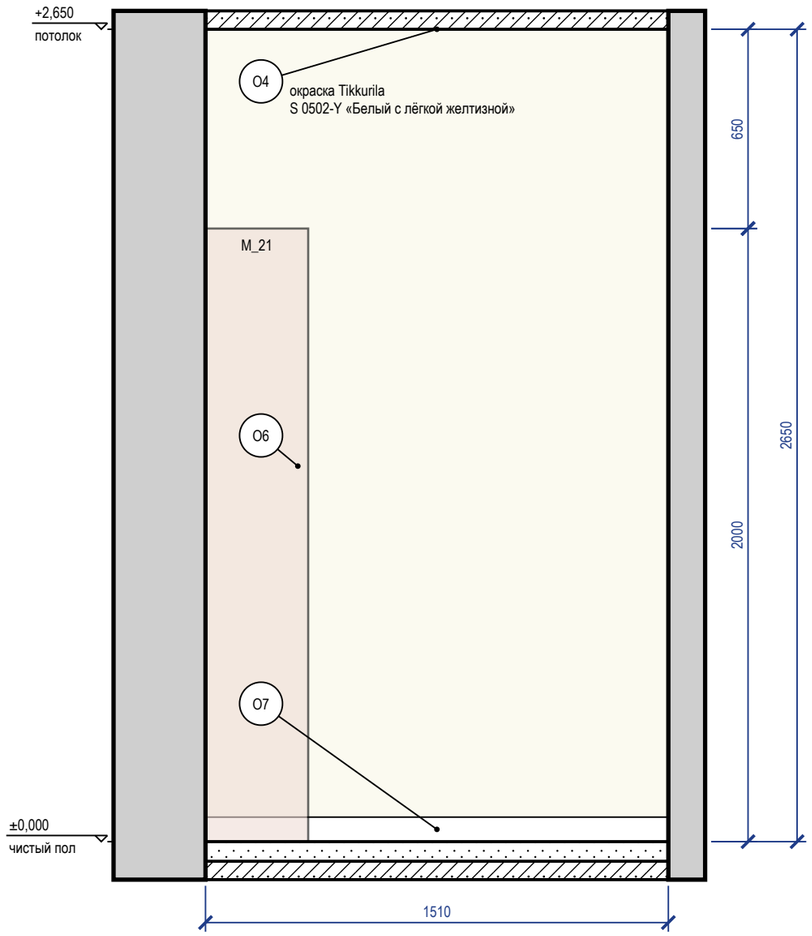

Развёртка стены В


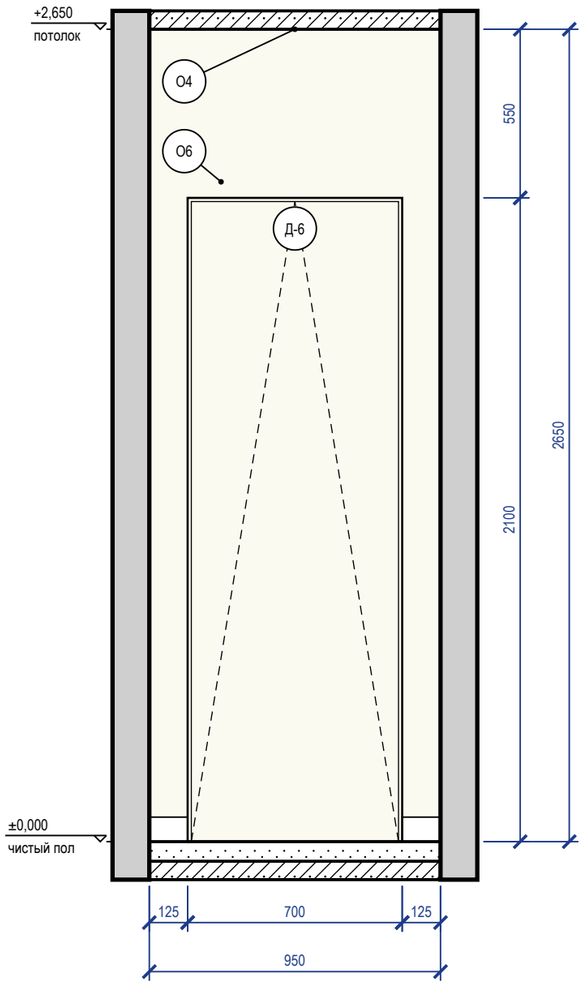


Схема развёрток (М 1:100)

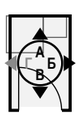

Ведомость отделки (на листе)

Марка	Поверхность	Материал, изделие	Цвет, код	Кол.
О4	потолок	окраска, Tikkurila Anti-Reflex 2, глубокоматовая, подготовка Q3	NCS S 0502-Y «Белый с лёгкой желтизной»	1,5 м²
О6	стены	окраска, Tikkurila Harmony, матовая, подготовка Q3	NCS S 0502-Y «Белый с лёгкой желтизной»	7,6 м²
О7	плинтус	плинтус МДФ, h 80 мм, аналог: плинтус МДФ под покраску 80×16	NCS S 0502-Y «Белый с лёгкой желтизной»	1,8 м

Визуализация этой стены — лист 67



Примечания

1. Размеры — в мм от чистовых поверхностей стен; условные обозначения и общие указания — лист 2.
2. Схема мебели, приборов и декора не является технической документацией для производства мебели; габариты — по паспортам изделий.
3. Выводы ВК — коды и высоты по листу выводов сантехники.
4. Двери скрытого монтажа — полотно в плоскости стены, отделка стены по полотну, плинтус прерывается у короба (узел — на листе узлов).

					Проект: Квартира 103 м²
	Лист	№ док.	Подпись	Дата	Развёртки стен А, Б, В. Постирочная (пом. 7)
Дизайнер	Кырлан А.С.			18.10.26	

Стадия	Лист	Листов
П	68	103

выпуск 18.10.2026 № d119044df4 · стр. 68 из 103

Развёртка стены Г


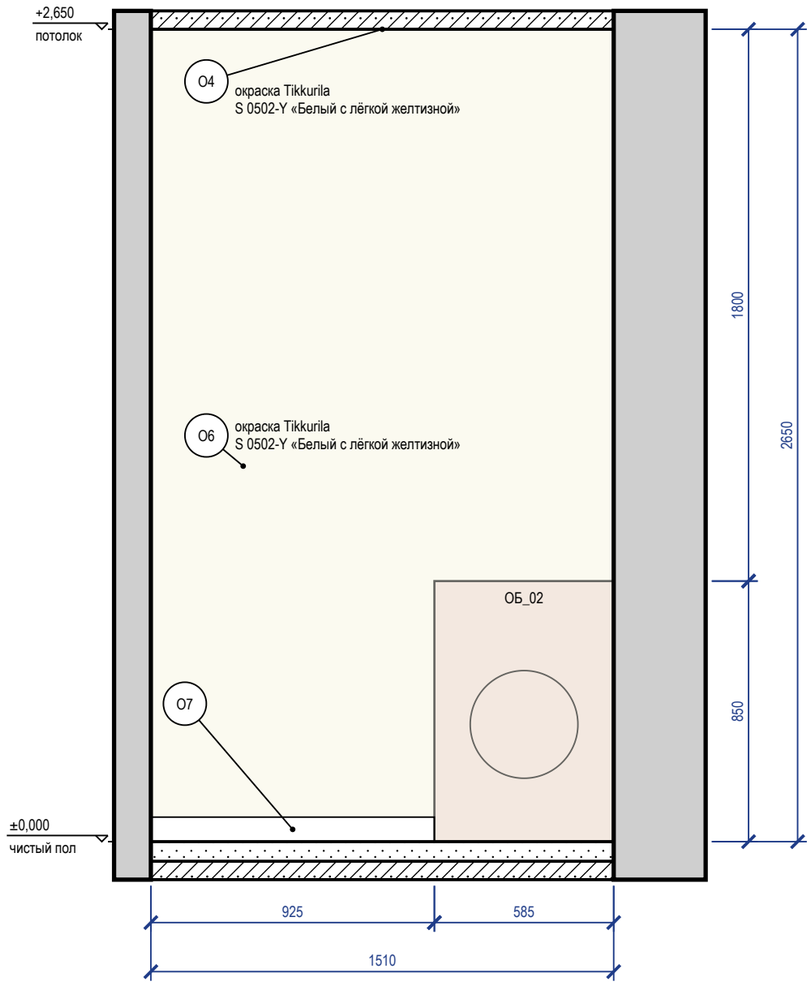


Схема развёрток (М 1:100)

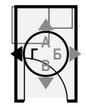

Ведомость отделки (на листе)

Марка	Поверхность	Материал, изделие	Цвет, код	Кол.
О4	потолок	окраска, Tikkurila Anti-Reflex 2, глубокоматовая, подготовка Q3	NCS S 0502-Y «Белый с лёгкой желтизной»	1,5 м²
О6	стены	окраска, Tikkurila Harmony, матовая, подготовка Q3	NCS S 0502-Y «Белый с лёгкой желтизной»	4 м²
О7	плинтус	плинтус МДФ, h 80 мм, аналог: плинтус МДФ под покраску 80×16	NCS S 0502-Y «Белый с лёгкой желтизной»	0,9 м


Примечания

1. Размеры — в мм от чистовых поверхностей стен; условные обозначения и общие указания — лист 2.
2. Схема мебели, приборов и декора не является технической документацией для производства мебели; габариты — по паспортам изделий.

					Проект: Квартира 103 м²
	Лист	№ док.	Подпись	Дата	Развёртка стены Г. Постирочная (пом. 7)
Дизайнер	Кырлан А.С.			18.10.26	

Стадия	Лист	Листов
П	69	103

выпуск 18.10.2026 № d119044df4 · стр. 69 из 103

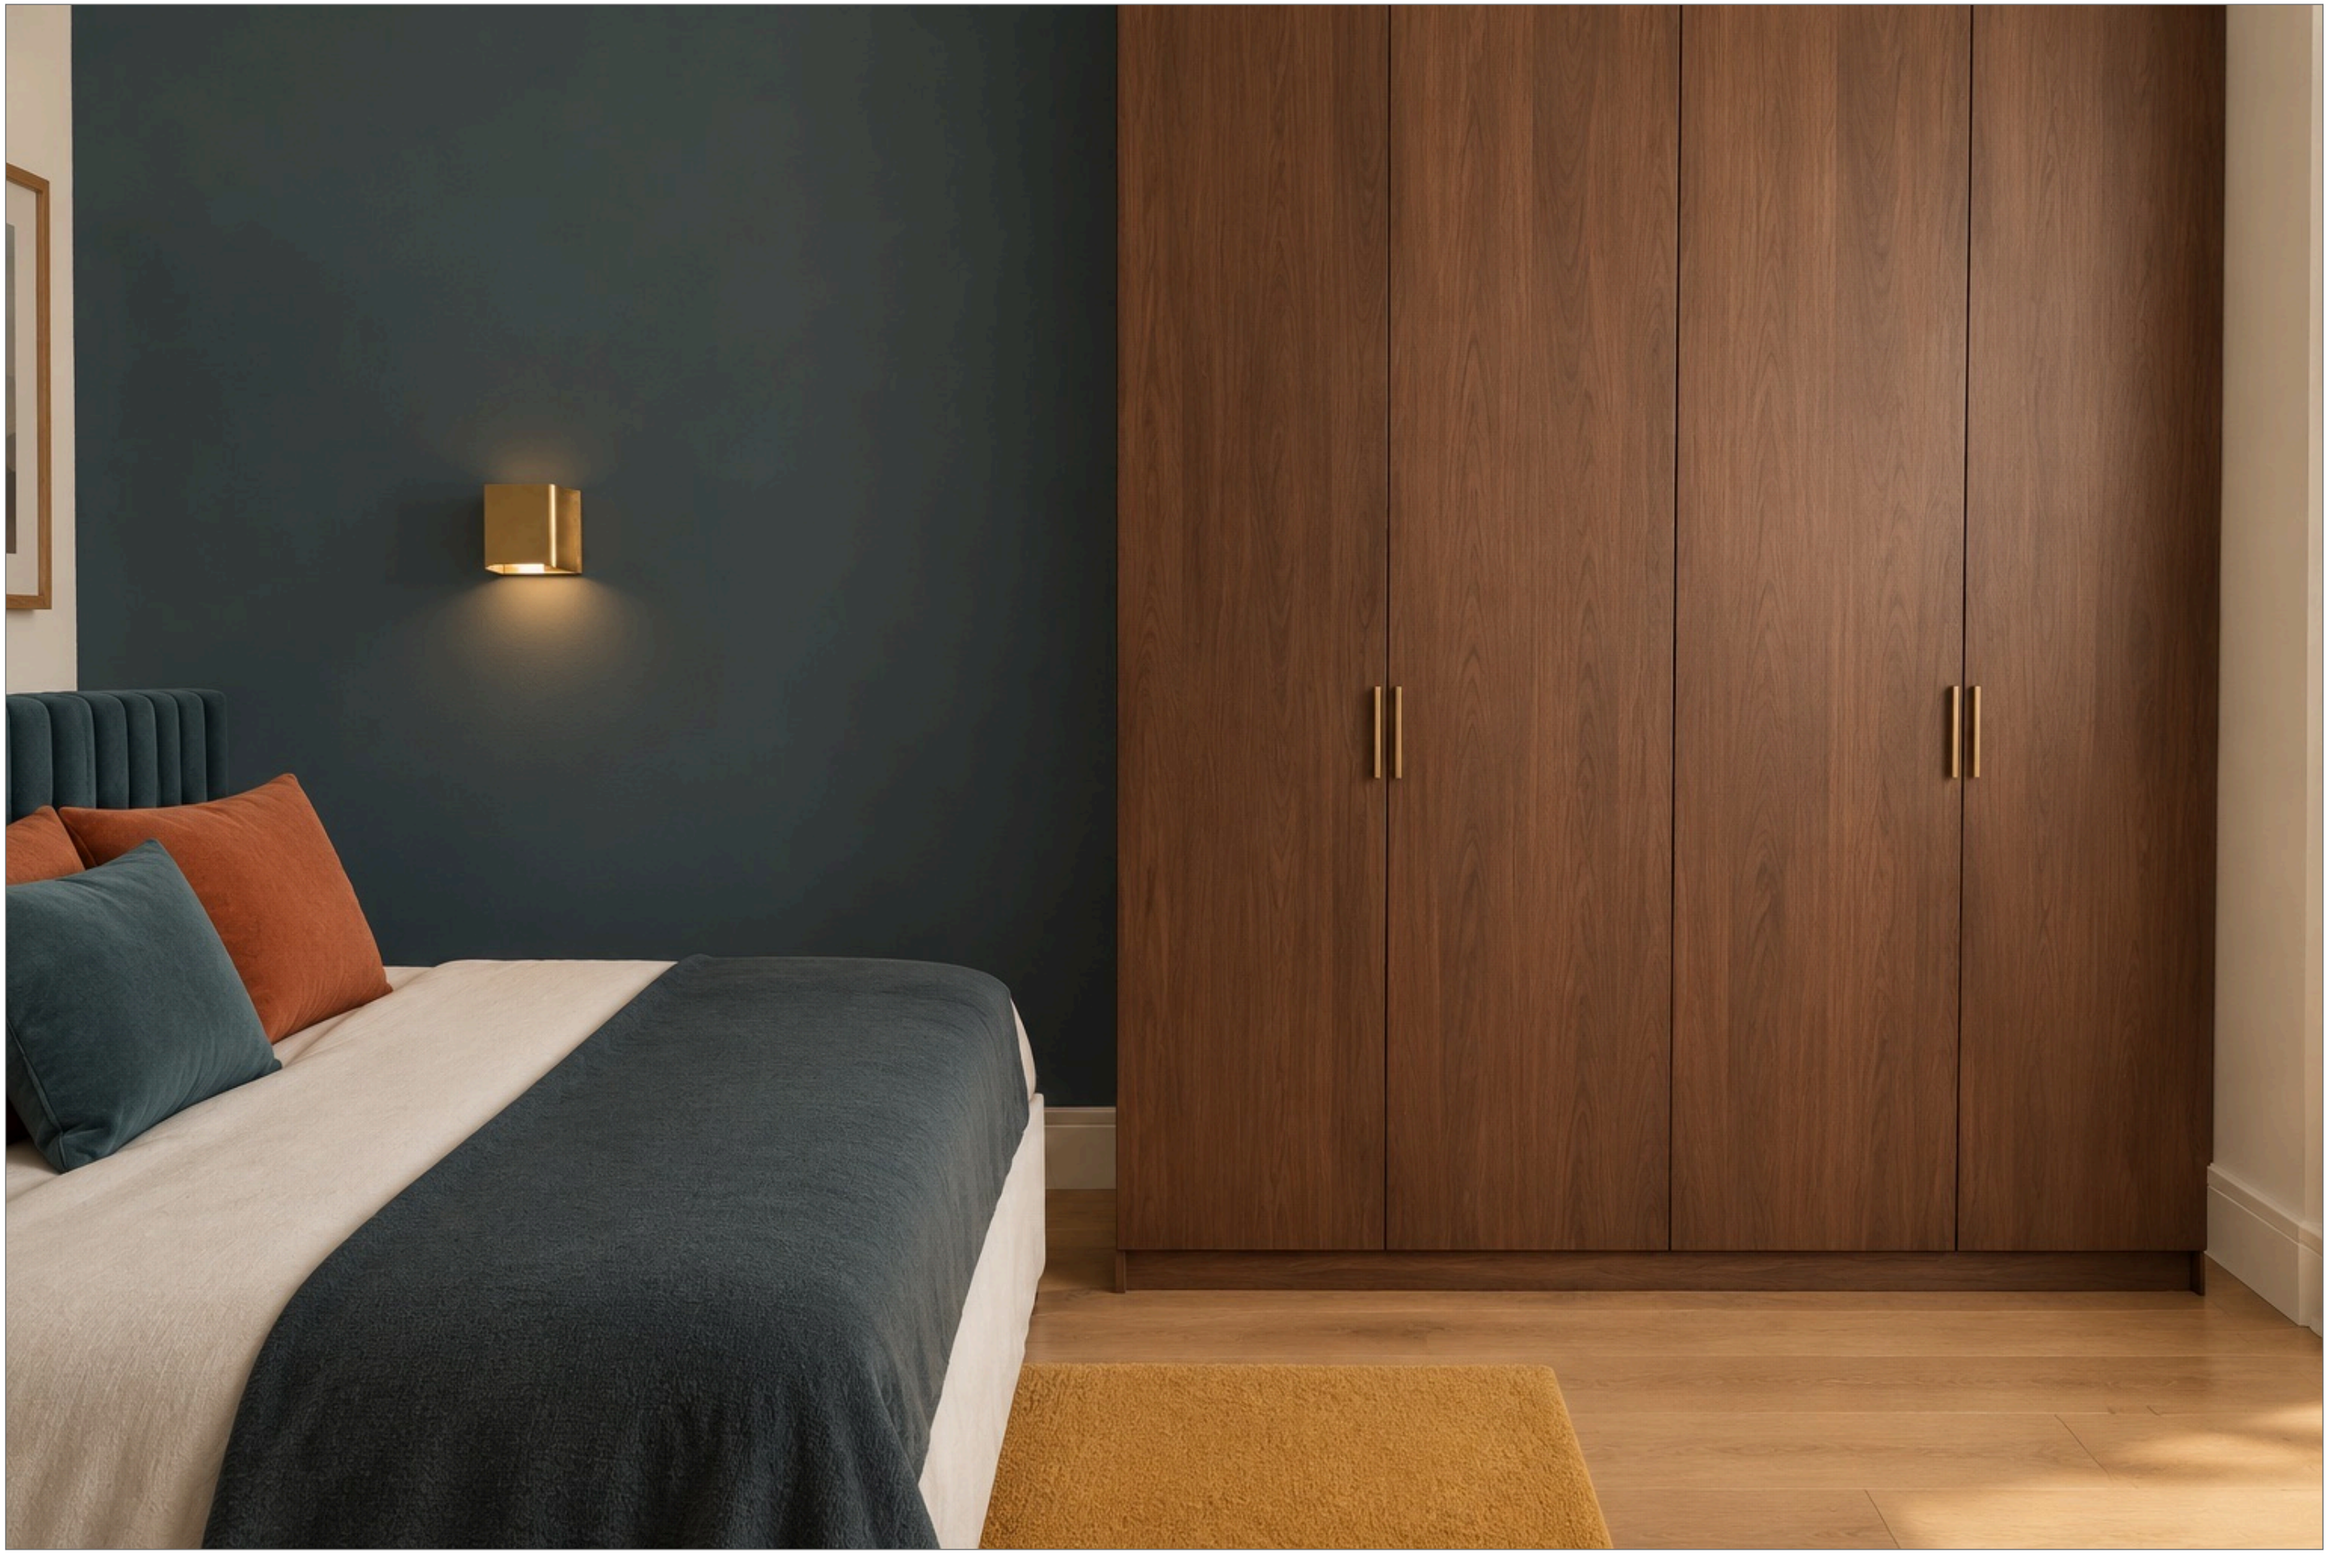

					Проект: Квартира 103 м²
	Лист	№ док.	Подпись	Дата	Визуализация: Спальня 2
Дизайнер	Кырлан А.С.			18.10.26	

Стадия	Лист	Листов
П	70	103

выпуск 18.10.2026 № d119044df4 · стр. 70 из 103



					Проект: Квартира 103 м²			
	Лист	№ док.	Подпись	Дата	Визуализация: Спальня 2	Стадия	Лист	Листов
Дизайнер	Кырлан А.С.			18.10.26				
						П	71	103

выпуск 18.10.2026 № d119044df4 · стр. 71 из 103



					Проект: Квартира 103 м²
	Лист	№ док.	Подпись	Дата	Визуализация: Спальня 2
Дизайнер	Кырлан А.С.			18.10.26	

Стадия	Лист	Листов
П	72	103

выпуск 18.10.2026 № d1190444df4 · стр. 72 из 103

Развёртка стены А


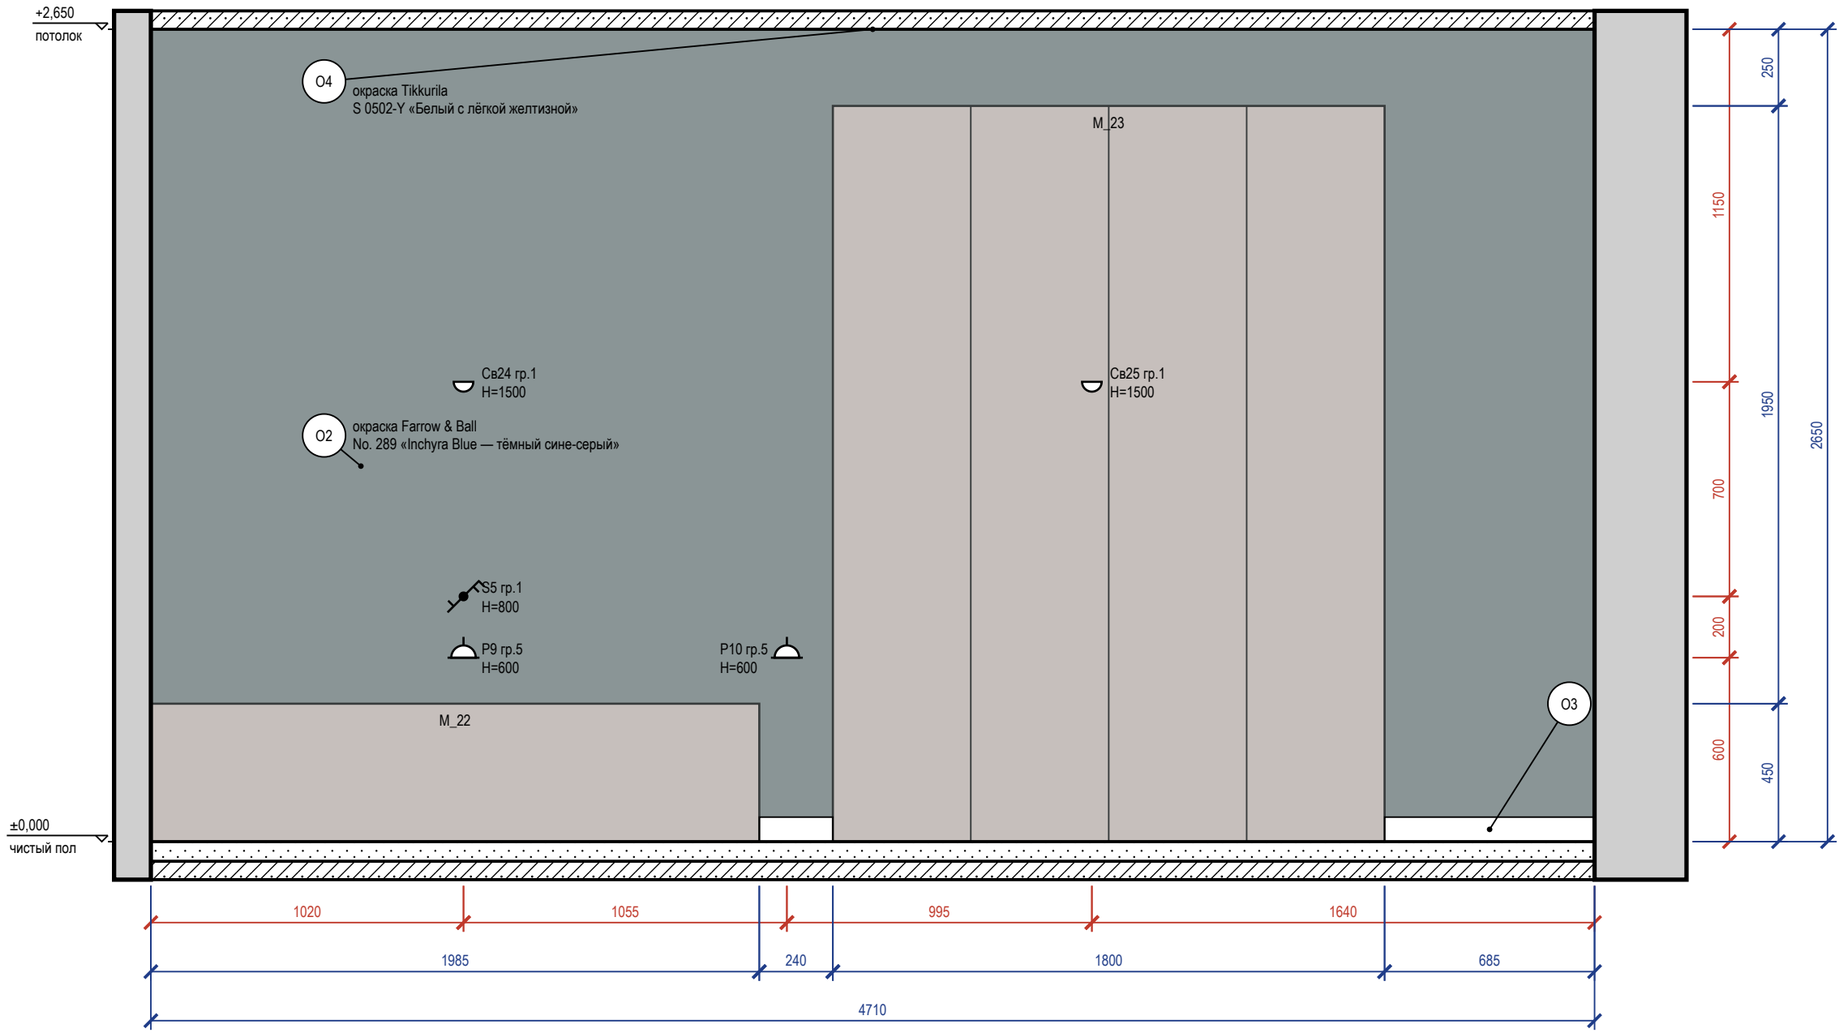



Схема развёрток (М 1:100)

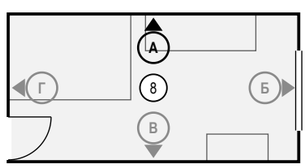

Ведомость отделки (на листе)

Марка	Поверхность	Материал, изделие	Цвет, код	Кол.
О2	акцентная стена	окраска, Farrow & Ball Modern Emulsion, матовая, подготовка Q3	Farrow & Ball No. 289 «Inchyra Blue — тёмный сине-серый»	12,5 м²
О3	плинтус	плинтус МДФ, h 80 мм, аналог: плинтус МДФ под покраску 80×16	Farrow & Ball No. 291 «School House White тёплый меловой белый»	0,9 м
О4	потолок	окраска, Tikkurila Anti-Reflex 2, глубокоматовая, подготовка Q3	NCS S 0502-Y «Белый с лёгкой желтизной»	11,4 м²

Визуализация этой стены — лист 70

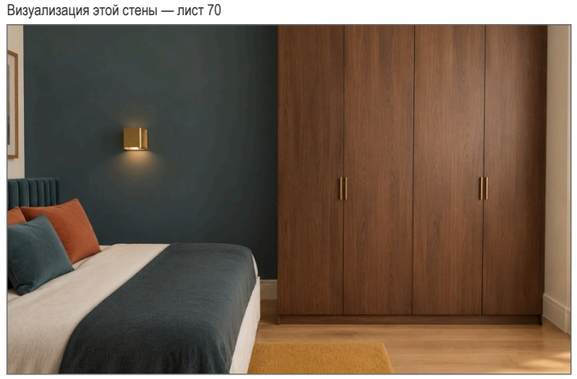

Примечания

1. Размеры — в мм от чистовых поверхностей стен; условные обозначения и общие указания — лист 2.

					Проект: Квартира 103 м²
	Лист	№ док.	Подпись	Дата	Развёртка стены А. Спальня 2 (пом. 8)
Дизайнер	Кырлан А.С.			18.10.26	

Стадия	Лист	Листов
П	73	103

выпуск 18.10.2026 № d119044df4 · стр. 73 из 103

Развёртка стены Б


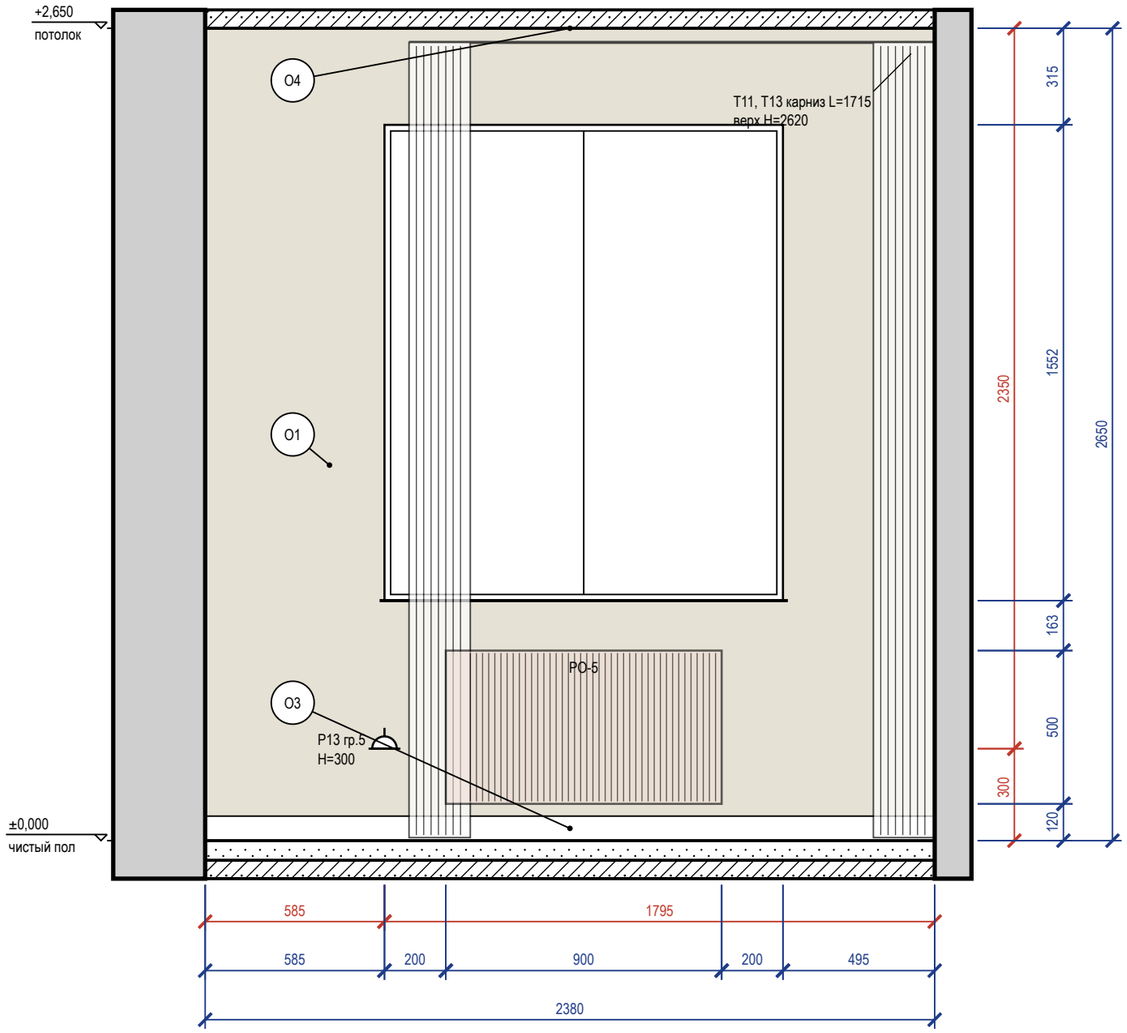


Схема развёрток (М 1:100)

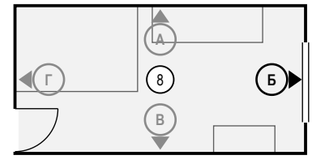

Ведомость отделки (на листе)

Марка	Поверхность	Материал, изделие	Цвет, код	Кол.
О1	стены	окраска, Farrow & Ball Modern Emulsion, матовая, подготовка Q3	Farrow & Ball No. 291 «School House White — тёплый меловой белый»	4,3 м²
О3	плинтус	плинтус МДФ, h 80 мм, аналог: плинтус МДФ под покраску 80×16	Farrow & Ball No. 291 «School House White — тёплый меловой белый»	2,4 м
О4	потолок	окраска, Tikkurila Anti-Reflex 2, глубокоматовая, подготовка Q3	NCS S 0502-Y «Белый с лёгкой желтизной»	11,4 м²

Визуализация этой стены — лист 71



Примечания

1. Размеры — в мм от чистовых поверхностей стен; условные обозначения и общие указания — лист 2.
2. Карнизы (шины) — по ведомости текстиля декоратора; длина L и верх Н — по развёртке, крепление — до окраски потолка.
3. Линии узора (швы плитки, складки штор, рёбра радиаторов) прерываются у знаков и выносок — просвет между линиями не менее 0,7 мм.

					Проект: Квартира 103 м²
	Лист	№ док.	Подпись	Дата	Развёртка стены Б. Спальня 2 (пом. 8)
Дизайнер	Кырлан А.С.			18.10.26	

Стадия	Лист	Листов
П	74	103

выпуск 18.10.2026 № d119044df4 · стр. 74 из 103

Развёртка стены В


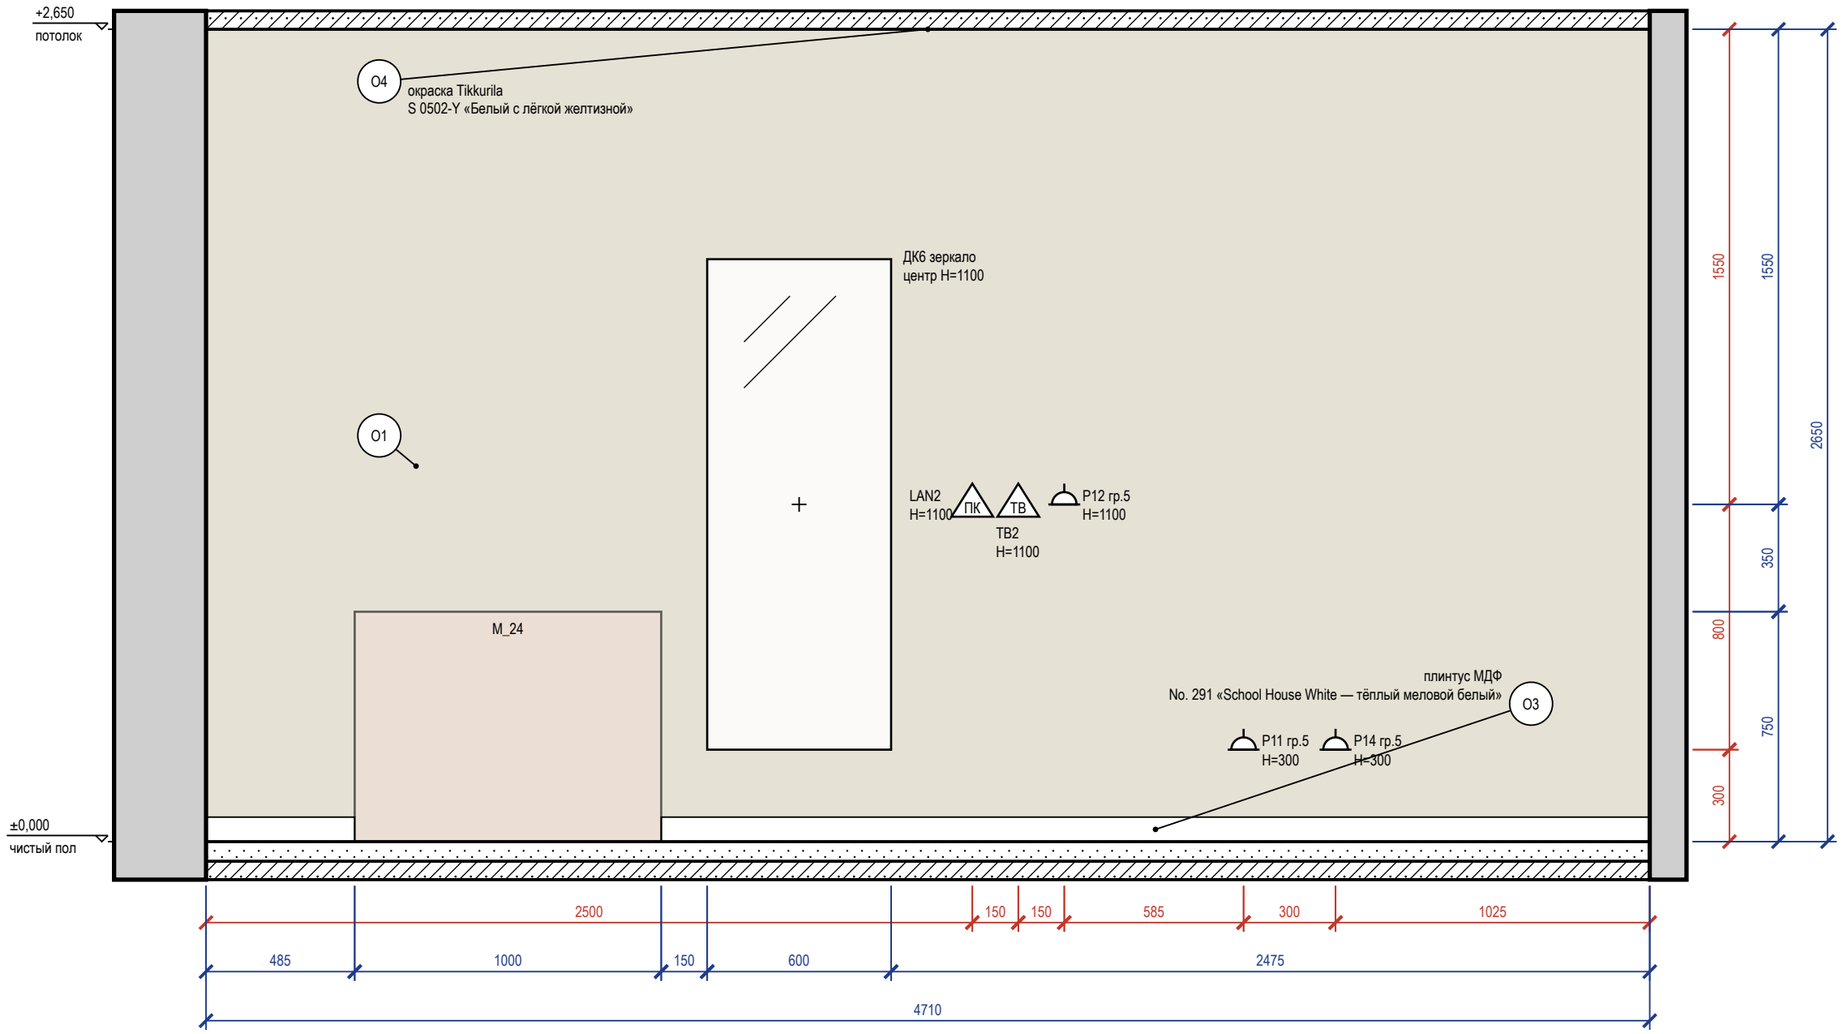


Схема развёрток (М 1:100)

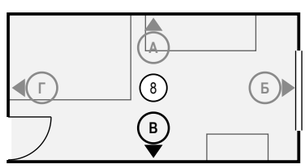

Ведомость отделки (на листе)

Марка	Поверхность	Материал, изделие	Цвет, код	Кол.
О1	стены	окраска, Farrow & Ball Modern Emulsion, матовая, подготовка Q3	Farrow & Ball No. 291 «School House White тёплый меловой белый»	12,5 м²
О3	плинтус	плинтус МДФ, h 80 мм, аналог: плинтус МДФ под покраску 80×16	Farrow & Ball No. 291 «School House White тёплый меловой белый»	3,7 м
О4	потолок	окраска, Tikkurila Anti-Reflex 2, глубокоматовая, подготовка Q3	NCS S 0502-Y «Белый с лёгкой желтизной»	11,4 м²

Примечания

1. Размеры — в мм от чистовых поверхностей стен; условные обозначения и общие указания — лист 2.
2. Картины и зеркала крепить к основанию по паспорту изделия (закладные и анкеры — в перечне скрытых работ); крест — ось центра предмета.

	Лист	№ док.	Подпись	Дата
Дизайнер	Кырлан А.С.			18.10.26

Проект: Квартира 103 м²

Развёртка стены В. Спальня 2 (пом. 8)

Стадия	Лист	Листов
П	75	103

выпуск 18.10.2026 № d119044df4 · стр. 75 из 103

Развёртка стены Г


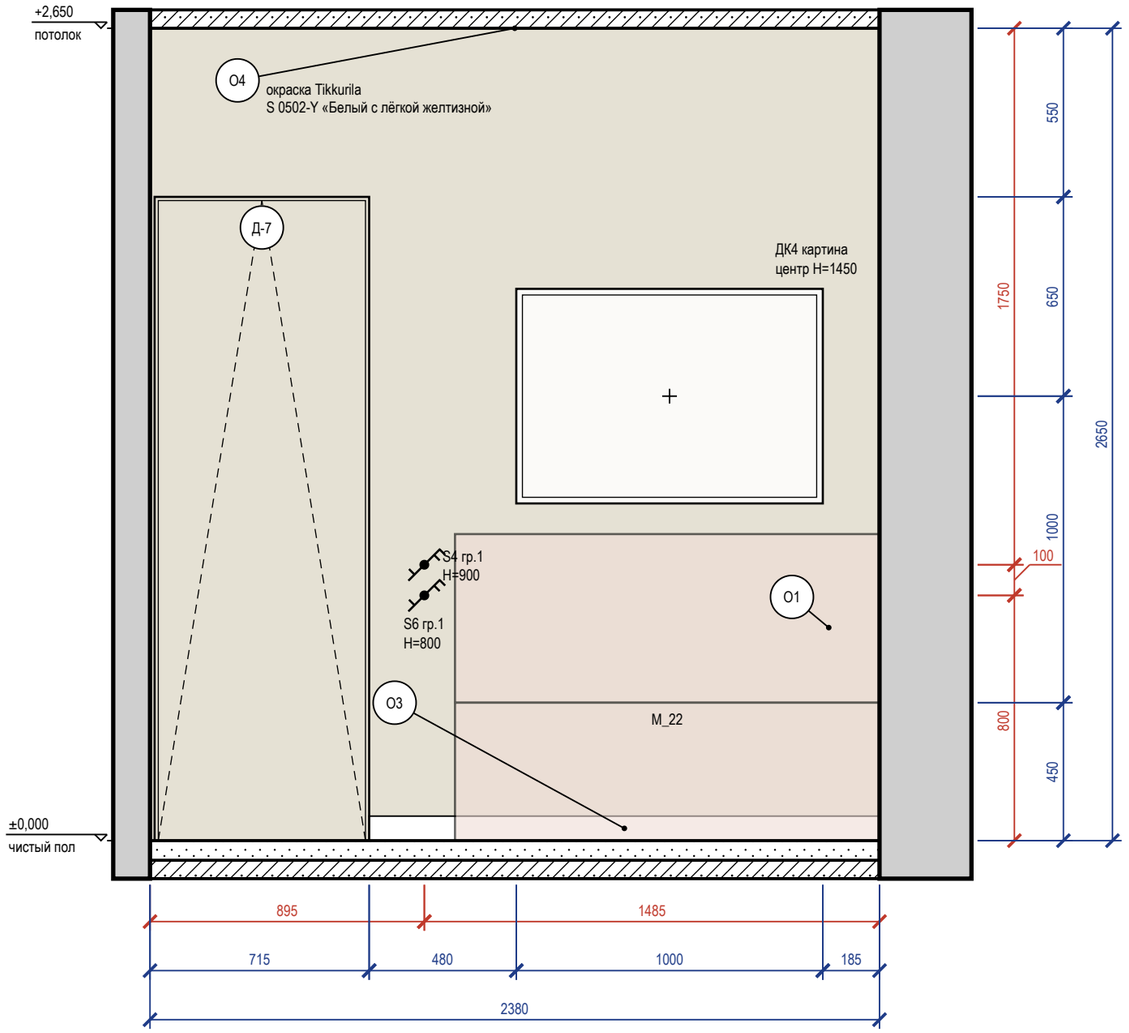


Схема развёрток (М 1:100)

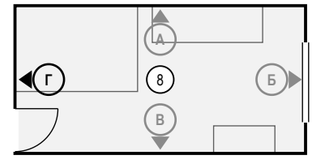

Ведомость отделки (на листе)

Марка	Поверхность	Материал, изделие	Цвет, код	Кол.
О1	стены	окраска, Farrow & Ball Modern Emulsion, матовая, подготовка Q3	Farrow & Ball No. 291 «School House White — тёплый меловой белый»	4,8 м²
О3	плинтус	плинтус МДФ, h 80 мм, аналог: плинтус МДФ под покраску 80×16	Farrow & Ball No. 291 «School House White — тёплый меловой белый»	1,7 м
О4	потолок	окраска, Tikkurila Anti-Reflex 2, глубокоматовая, подготовка Q3	NCS S 0502-Y «Белый с лёгкой желтизной»	11,4 м²

Визуализация этой стены — лист 72



Примечания

1. Размеры — в мм от чистовых поверхностей стен; условные обозначения и общие указания — лист 2.
2. Картины и зеркала крепить к основанию по паспорту изделия (закладные и анкеры — в перечне скрытых работ); крест — ось центра предмета.
3. Двери скрытого монтажа — полотно в плоскости стены, отделка стены по полотну, плинтус прерывается у короба (узел — на листе узлов).

					Проект: Квартира 103 м²
	Лист	№ док.	Подпись	Дата	
Дизайнер	Кырлан А.С.			18.10.26	Развёртка стены Г. Спальня 2 (пом. 8)

Стадия	Лист	Листов
П	76	103

выпуск 18.10.2026 № d119044df4 · стр. 76 из 103



					Проект: Квартира 103 м²	
	Лист	№ док.	Подпись	Дата	Визуализация коридора	Стадия / Лист / Листов
Дизайнер	Кырлан А.С.			18.10.26		П / 77 / 103

выпуск 18.10.2026 № d119044df4 · стр. 77 из 103

Развёртка стены А


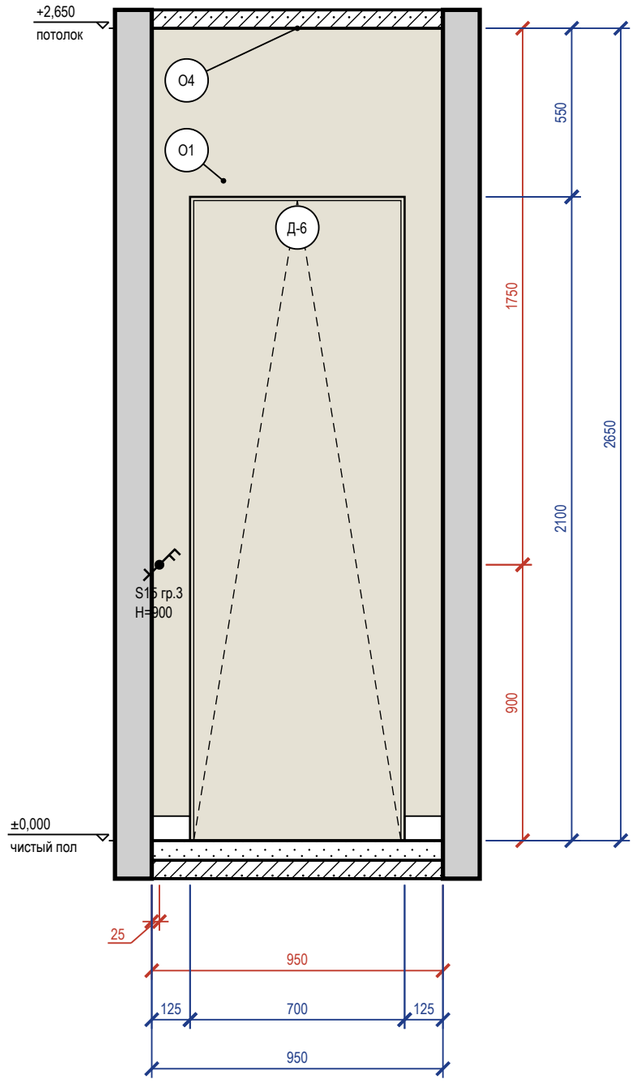


Схема развёрток (М 1:100)

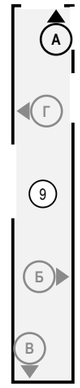

Ведомость отделки (на листе)

Марка	Поверхность	Материал, изделие	Цвет, код	Кол.
О1	стены	окраска, Farrow & Ball Modern Emulsion, матовая, подготовка Q3	Farrow & Ball No. 291 «School House White — тёплый меловой белый»	1 м²
О3	плинтус	плинтус МДФ, h 80 мм, аналог: плинтус МДФ под покраску 80×16	Farrow & Ball No. 291 «School House White — тёплый меловой белый»	0,3 м
О4	потолок	окраска, Tikkurila Anti-Reflex 2, глубокоматовая, подготовка Q3	NCS S 0502-Y «Белый с лёгкой желтизной»	6 м²

Примечания

1. Размеры — в мм от чистовых поверхностей стен; условные обозначения и общие указания — лист 2.
2. Двери скрытого монтажа — полотно в плоскости стены, отделка стены по полотну, плинтус прерывается у короба (узел — на листе узлов).

	Лист	№ док.	Подпись	Дата
Дизайнер	Кырлан А.С.			18.10.26

Проект: Квартира 103 м²

Развёртка стены А. Коридор (пом. 9)

Стадия	Лист	Листов
П	78	103

выпуск 18.10.2026 № d119044df4 · стр. 78 из 103

Развёртка стены Б


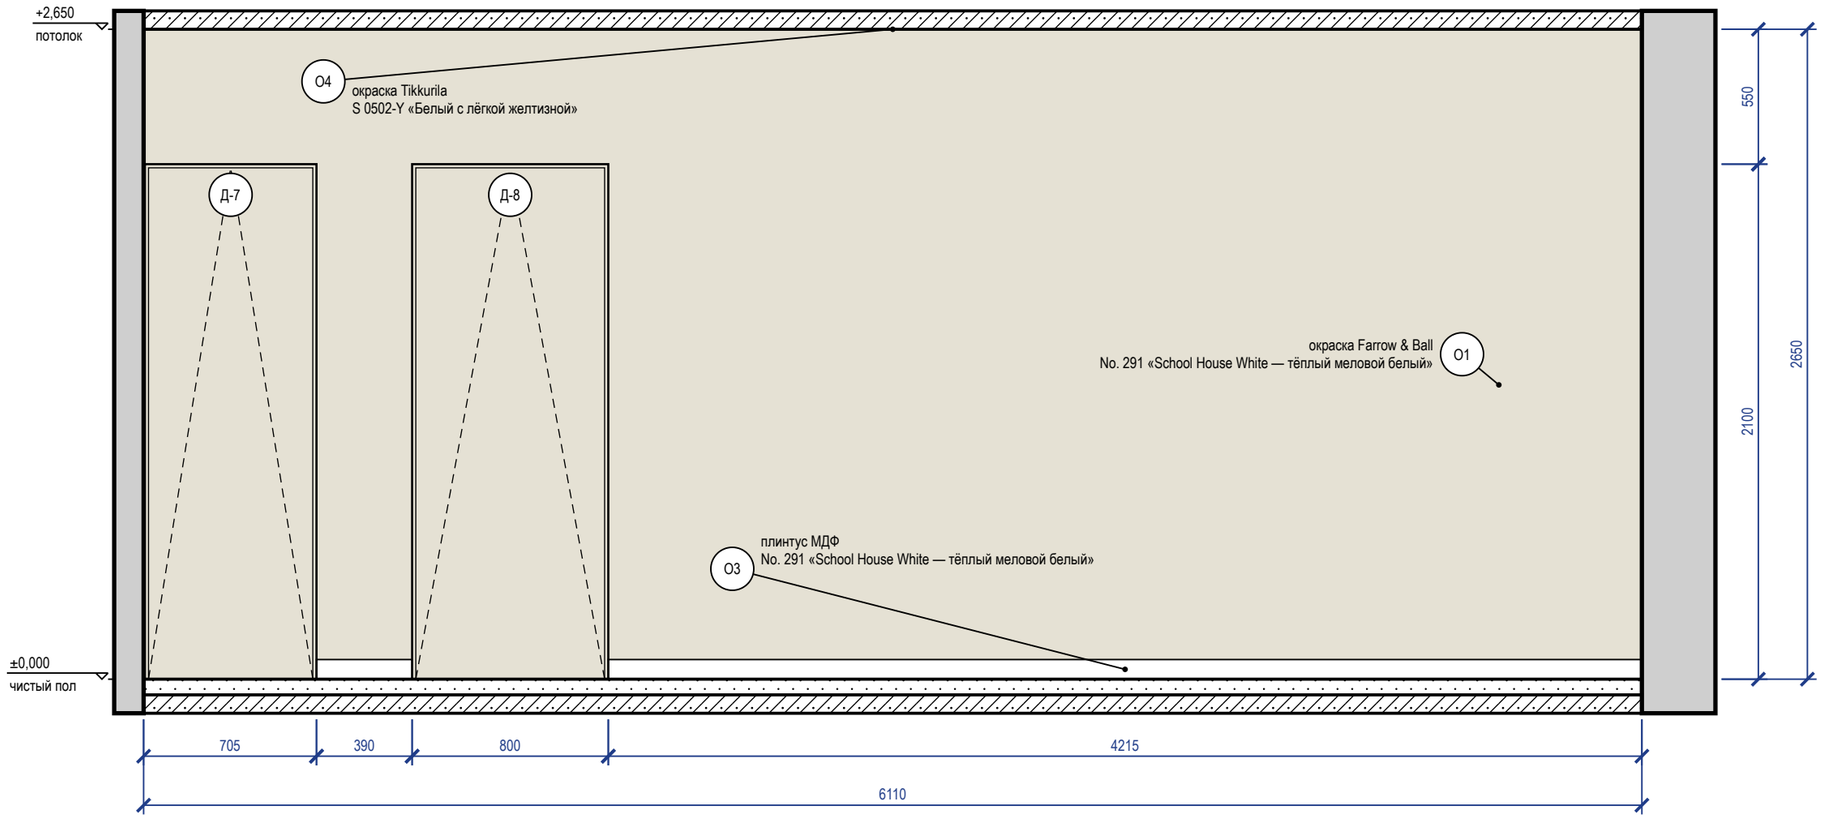


Схема развёрток (М 1:100)

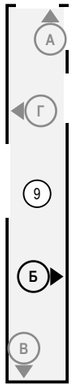

Ведомость отделки (на листе)

Марка	Поверхность	Материал, изделие	Цвет, код	Кол.
О1	стены	окраска, Farrow & Ball Modern Emulsion, матовая, подготовка Q3	Farrow & Ball No. 291 «School House White тёплый меловой белый»	13 м²
О3	плинтус	плинтус МДФ, h 80 мм, аналог: плинтус МДФ под покраску 80×16	Farrow & Ball No. 291 «School House White тёплый меловой белый»	4,6 м
О4	потолок	окраска, Tikkurila Anti-Reflex 2, глубокоматовая, подготовка Q3	NCS S 0502-Y «Белый с лёгкой желтизной»	6 м²

Визуализация этой стены — лист 77



Примечания

1. Размеры — в мм от чистовых поверхностей стен; условные обозначения и общие указания — лист 2.
2. Двери скрытого монтажа — полотно в плоскости стены, отделка стены по полотну, плинтус прерывается у короба (узел — на листе узлов).

					Проект: Квартира 103 м²
	Лист	№ док.	Подпись	Дата	Развёртка стены Б. Коридор (пом. 9)
Дизайнер	Кырлан А.С.			18.10.26	

Стадия	Лист	Листов
П	79	103

выпуск 18.10.2026 № d119044df4 · стр. 79 из 103

Развёртка стены В


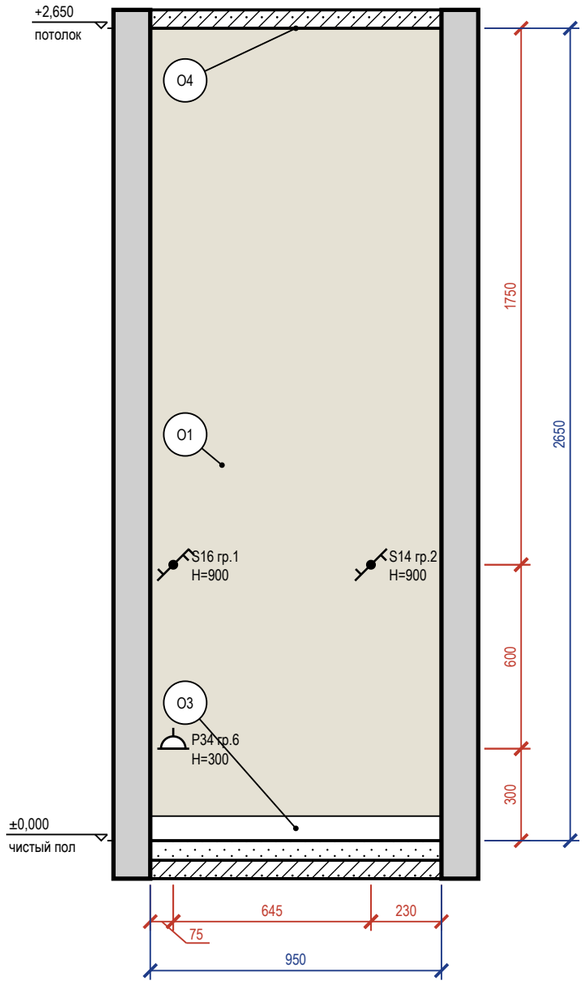


Схема развёрток (М 1:100)

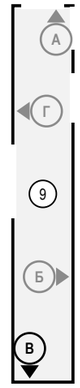

Ведомость отделки (на листе)

Марка	Поверхность	Материал, изделие	Цвет, код	Кол.
О1	стены	окраска, Farrow & Ball Modern Emulsion, матовая, подготовка Q3	Farrow & Ball No. 291 «School House White — тёплый меловой белый»	2,5 м²
О3	плинтус	плинтус МДФ, h 80 мм, аналог: плинтус МДФ под покраску 80×16	Farrow & Ball No. 291 «School House White — тёплый меловой белый»	0,9 м
О4	потолок	окраска, Tikkurila Anti-Reflex 2, глубокоматовая, подготовка Q3	NCS S 0502-Y «Белый с лёгкой желтизной»	6 м²

Примечания

1. Размеры — в мм от чистовых поверхностей стен; условные обозначения и общие указания — лист 2.

	Лист	№ док.	Подпись	Дата
Дизайнер	Кырлан А.С.			18.10.26

Проект: Квартира 103 м²

Развёртка стены В. Коридор (пом. 9)

Стадия	Лист	Листов
П	80	103

выпуск 18.10.2026 № d119044df4 · стр. 80 из 103

Развёртка стены Г


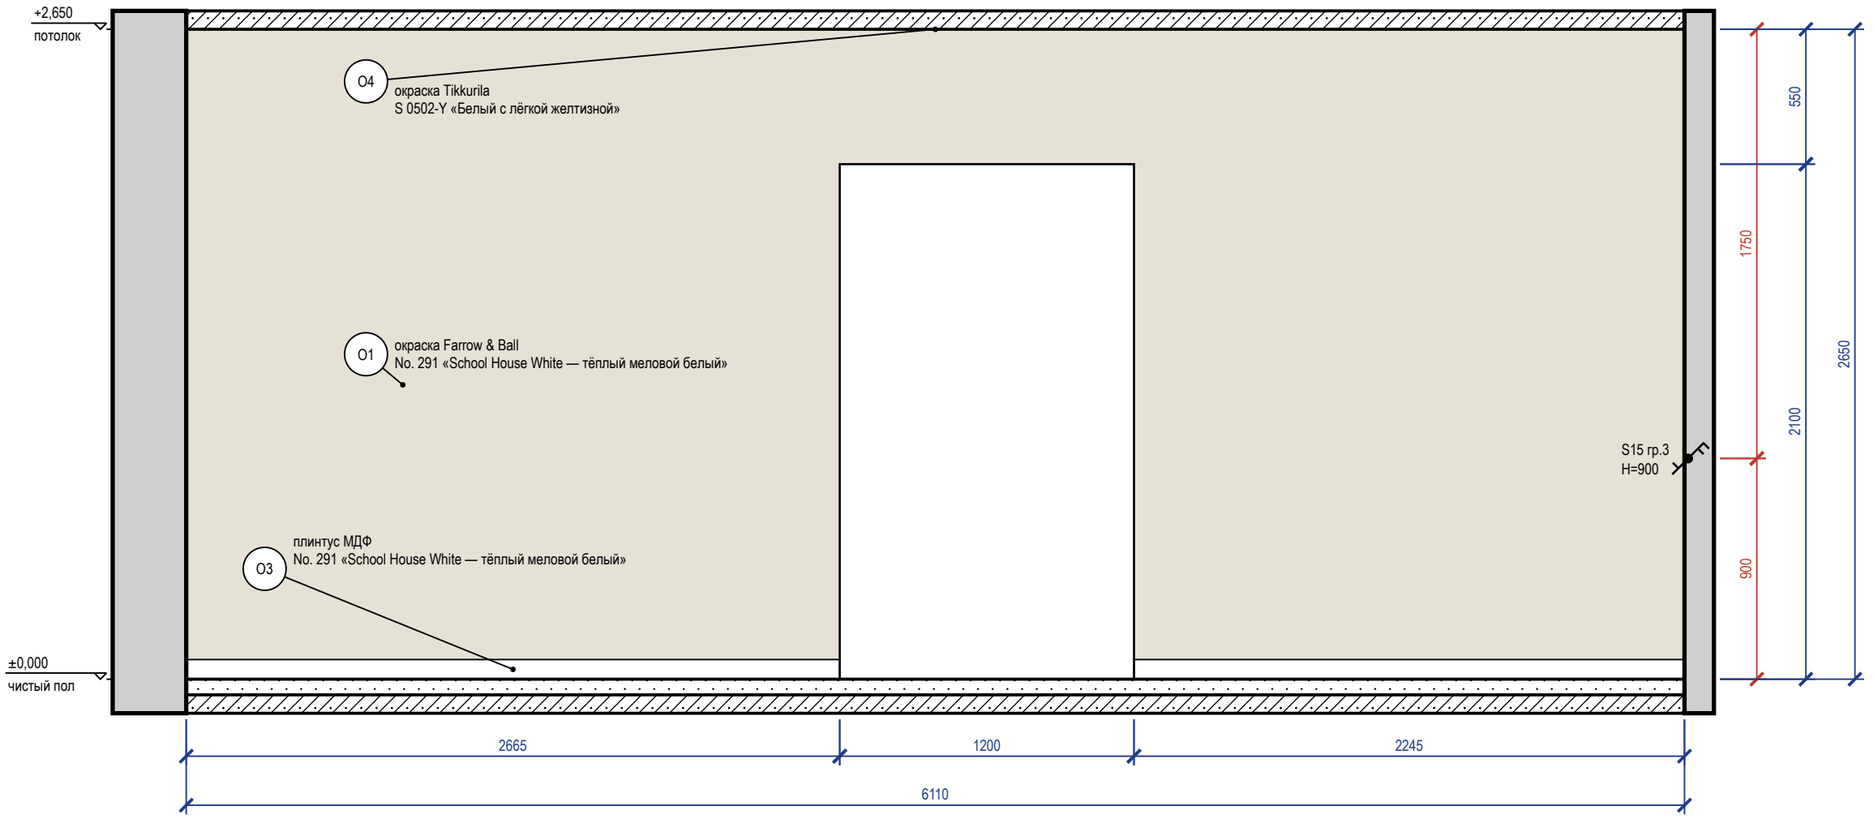


Схема развёрток (М 1:100)

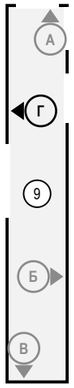

Ведомость отделки (на листе)

Марка	Поверхность	Материал, изделие	Цвет, код	Кол.
О1	стены	окраска, Farrow & Ball Modern Emulsion, матовая, подготовка Q3	Farrow & Ball No. 291 «School House White тёплый меловой белый»	13,7 м²
О3	плинтус	плинтус МДФ, h 80 мм, аналог: плинтус МДФ под покраску 80×16	Farrow & Ball No. 291 «School House White тёплый меловой белый»	4,9 м
О4	потолок	окраска, Tikkurila Anti-Reflex 2, глубокоматовая, подготовка Q3	NCS S 0502-Y «Белый с лёгкой желтизной»	6 м²

Примечания

1. Размеры — в мм от чистовых поверхностей стен; условные обозначения и общие указания — лист 2.

					Проект: Квартира 103 м²
	Лист	№ док.	Подпись	Дата	Развёртка стены Г. Коридор (пом. 9)
Дизайнер	Кырлан А.С.			18.10.26	

Стадия	Лист	Листов
П	81	103

выпуск 18.10.2026 № d119044df4 · стр. 81 из 103



					Проект: Квартира 103 м²
	Лист	№ док.	Подпись	Дата	
Дизайнер	Кырлан А.С.			18.10.26	Визуализация: Спальня мастер

Стадия	Лист	Листов
П	82	103

выпуск 18.10.2026 № d119044df4 · стр. 82 из 103



					Проект: Квартира 103 м²	
	Лист	№ док.	Подпись	Дата	Визуализация: Спальня мастер	Стадия / Лист / Листов
Дизайнер	Кырлан А.С.			18.10.26		П / 83 / 103

выпуск 18.10.2026 № d119044df4 · стр. 83 из 103



					Проект: Квартира 103 м²
	Лист	№ док.	Подпись	Дата	
Дизайнер	Кырлан А.С.			18.10.26	Визуализация: Спальня мастер

Стадия	Лист	Листов
П	84	103

выпуск 18.10.2026 · d119044df4 · стр. 84 из 103



					Проект: Квартира 103 м²
	Лист	№ док.	Подпись	Дата	
Дизайнер	Кырлан А.С.			18.10.26	Визуализация: Спальня мастер

Стадия	Лист	Листов
П	85	103

выпуск 18.10.2026 d119044df4 · стр. 85 из 103

Развёртка стены А


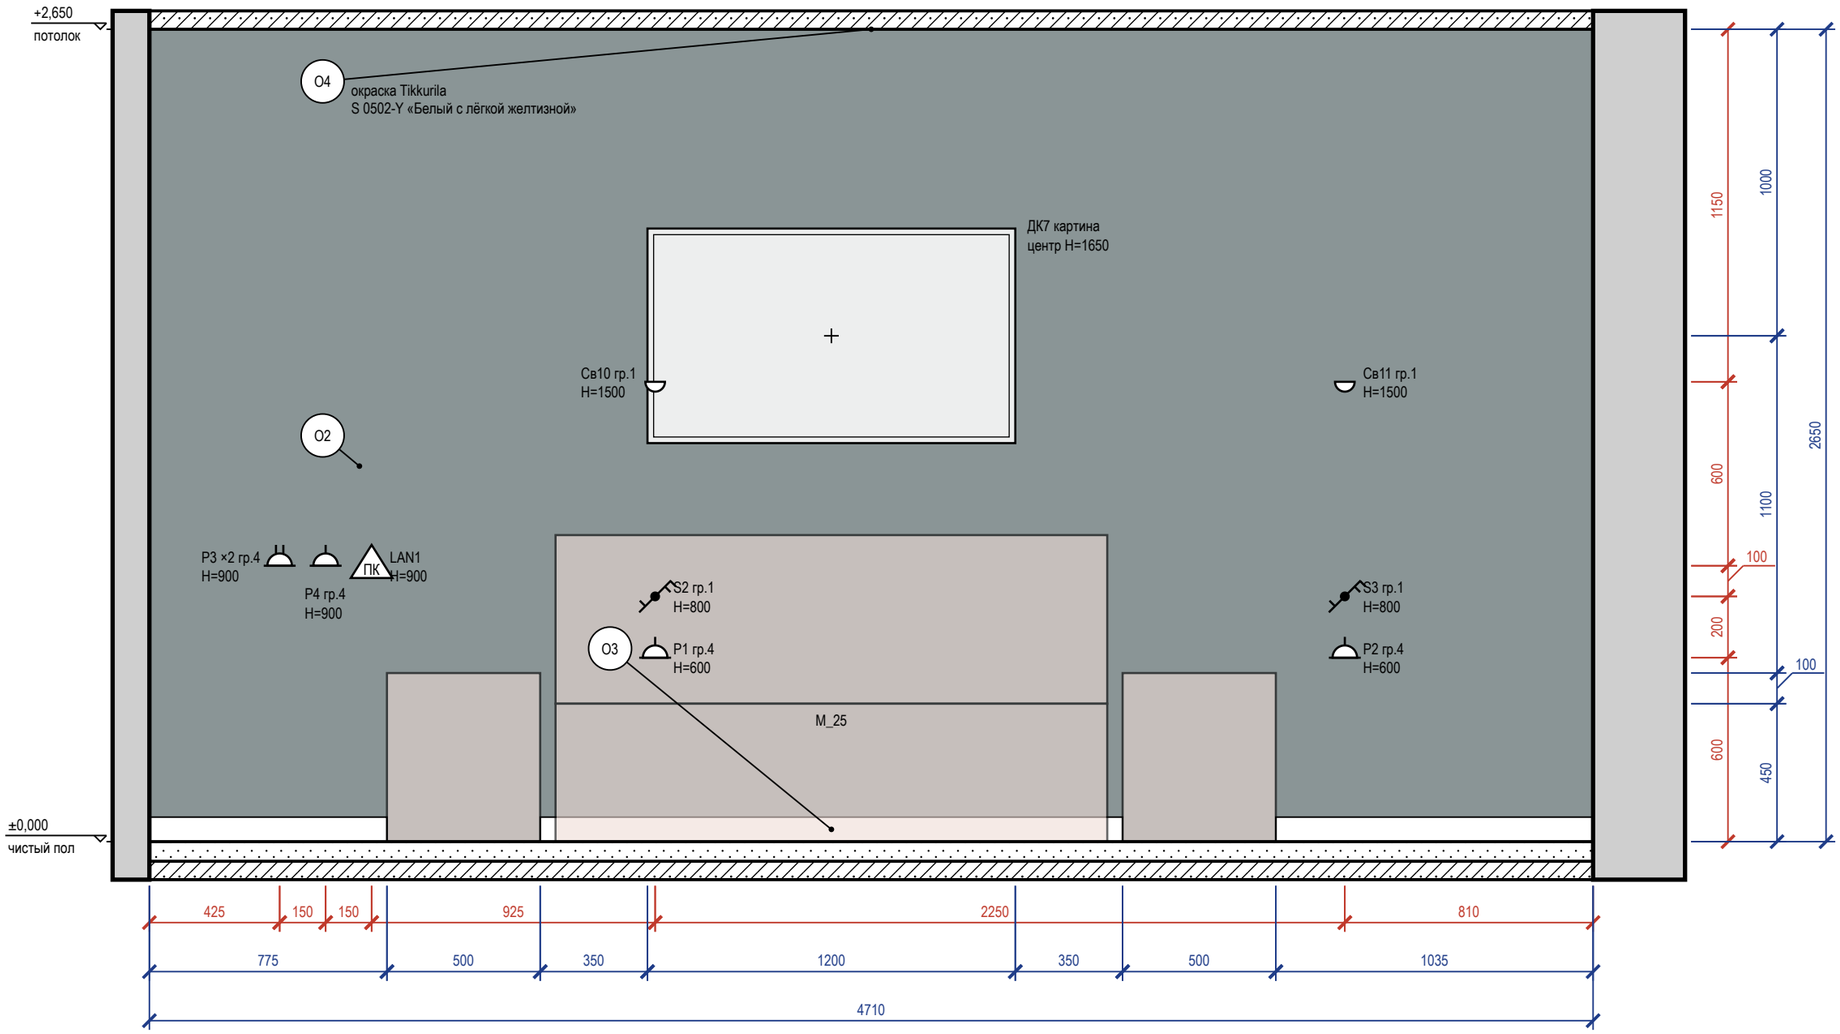



Схема развёрток (М 1:100)

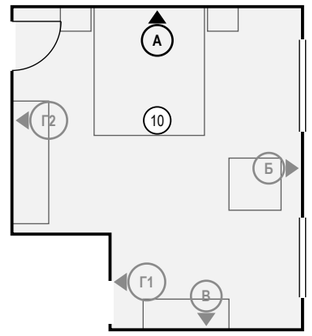

Ведомость отделки (на листе)

Марка	Поверхность	Материал, изделие	Цвет, код	Кол.
О2	акцентная стена	окраска, Farrow & Ball Modern Emulsion, матовая, подготовка Q3	Farrow & Ball No. 289 «Inchyra Blue — тёмный сине-серый»	12,5 м²
О3	плинтус	плинтус МДФ, h 80 мм, аналог: плинтус МДФ под покраску 80×16	Farrow & Ball No. 291 «School House White тёплый меловой белый»	3,7 м
О4	потолок	окраска, Tikkurila Anti-Reflex 2, глубокоматовая, подготовка Q3	NCS S 0502-Y «Белый с лёгкой желтизной»	22,5 м²

Визуализация этой стены — лист 82

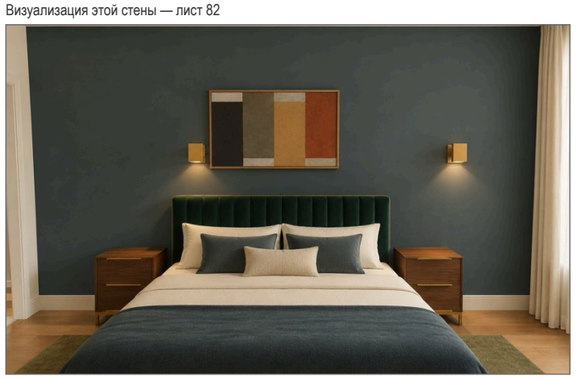

Примечания

1. Размеры — в мм от чистовых поверхностей стен; условные обозначения и общие указания — лист 2.
2. Картины и зеркала крепить к основанию по паспорту изделия (закладные и анкеры — в перечне скрытых работ); крест — ось центра предмета.

					Проект: Квартира 103 м²
	Лист	№ док.	Подпись	Дата	Развёртка стены А. Спальня мастер (пом. 10)
Дизайнер	Кырлан А.С.			18.10.26	

Стадия	Лист	Листов
П	86	103

выпуск 18.10.2026 № d119044df4 · стр. 86 из 103

Развёртка стены Б


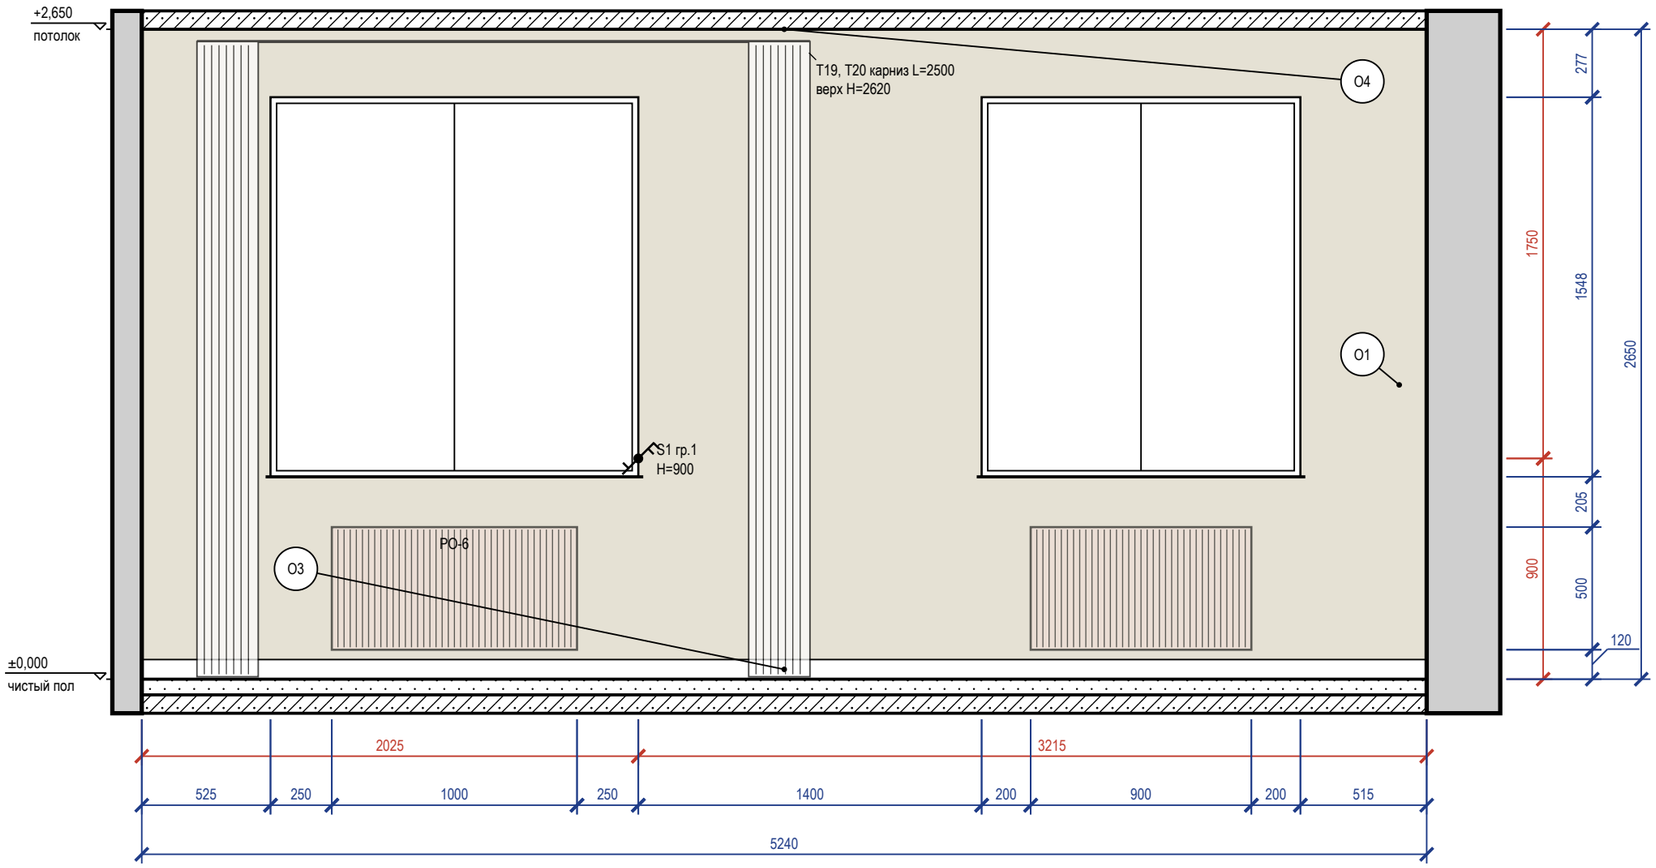


Схема развёрток (М 1:100)

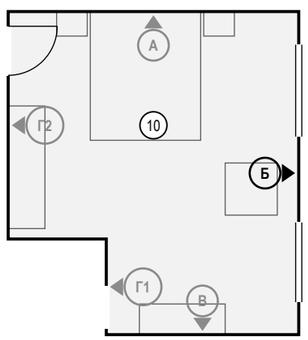

Ведомость отделки (на листе)

Марка	Поверхность	Материал, изделие	Цвет, код	Кол.
О1	стены	окраска, Farrow & Ball Modern Emulsion, матовая, подготовка Q3	Farrow & Ball No. 291 «School House White тёплый меловой белый»	9,6 м²
О3	плинтус	плинтус МДФ, h 80 мм, аналог: плинтус МДФ под покраску 80×16	Farrow & Ball No. 291 «School House White тёплый меловой белый»	5,2 м
О4	потолок	окраска, Tikkurila Anti-Reflex 2, глубокоматовая, подготовка Q3	NCS S 0502-Y «Белый с лёгкой желтизной»	22,5 м²

Визуализация этой стены — лист 83



Примечания

1. Размеры — в мм от чистовых поверхностей стен; условные обозначения и общие указания — лист 2.
2. Карнизы (шины) — по ведомости текстиля декоратора; длина L и верх H — по развёртке, крепление — до окраски потолка.

					Проект: Квартира 103 м²
	Лист	№ док.	Подпись	Дата	Развёртка стены Б. Спальня мастер (пом. 10)
Дизайнер	Кырлан А.С.			18.10.26	

Стадия	Лист	Листов
П	87	103

выпуск 18.10.2026 № d119044df4 · стр. 87 из 103

Развёртка стены В


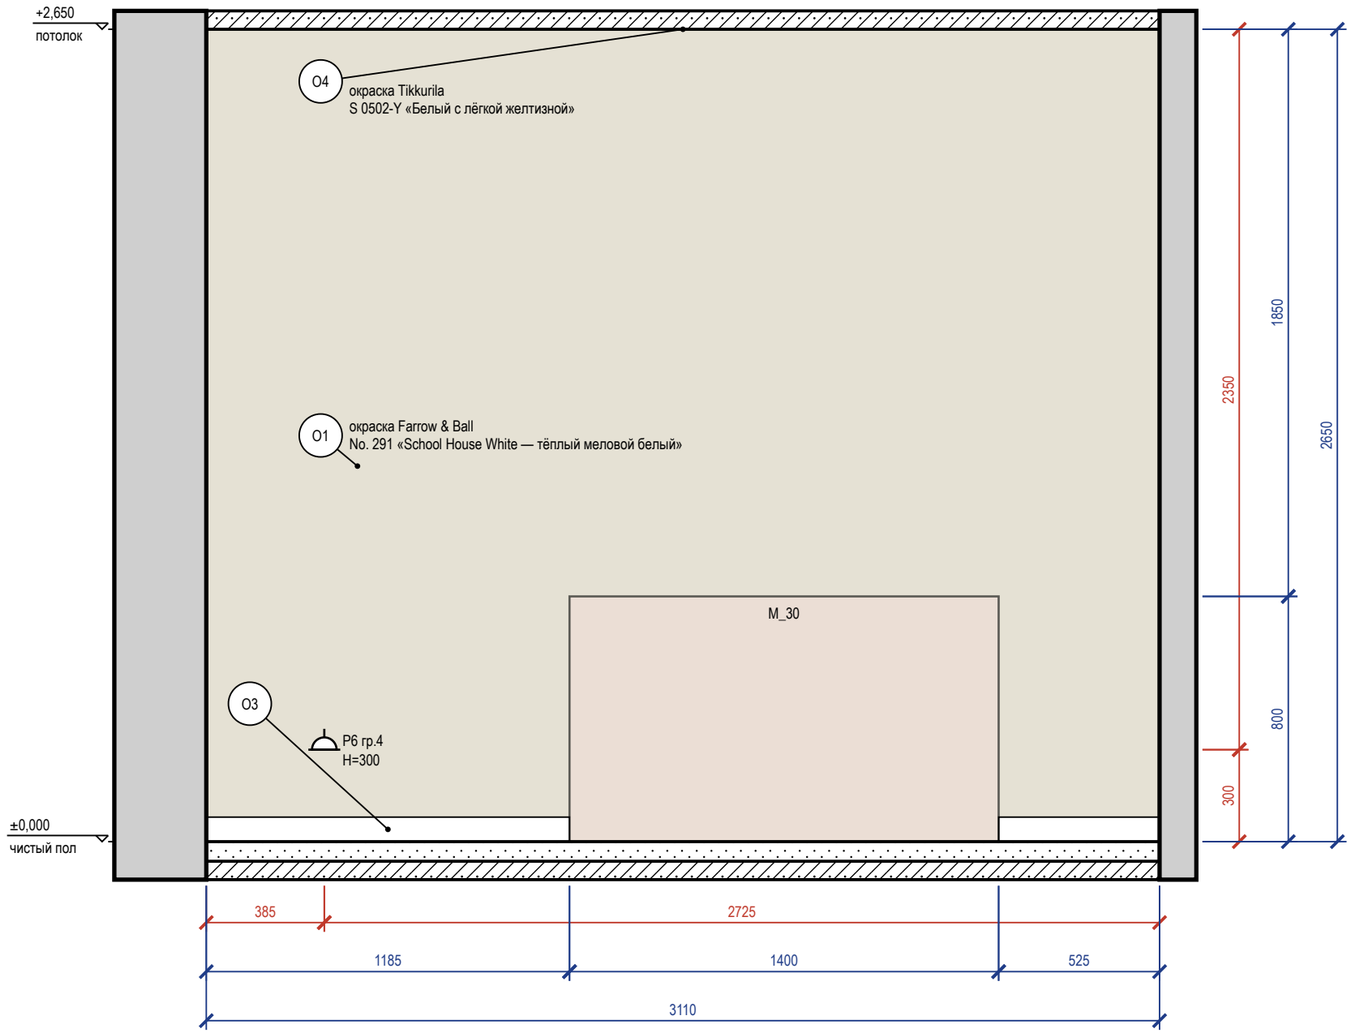


Схема развёрток (М 1:100)

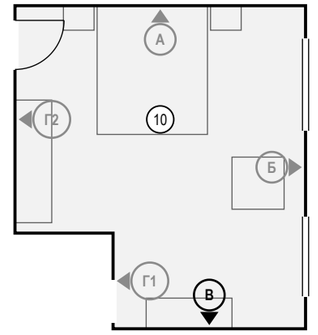


Ведомость отделки (на листе)

Марка	Поверхность	Материал, изделие	Цвет, код	Кол.
О1	стены	окраска, Farrow & Ball Modern Emulsion, матовая, подготовка Q3	Farrow & Ball No. 291 «School House White — тёплый меловой белый»	8,2 м²
О3	плинтус	плинтус МДФ, h 80 мм, аналог: плинтус МДФ под покраску 80×16	Farrow & Ball No. 291 «School House White — тёплый меловой белый»	1,7 м
О4	потолок	окраска, Tikkurila Anti-Reflex 2, глубокоматовая, подготовка Q3	NCS S 0502-Y «Белый с лёгкой желтизной»	22,5 м²

Визуализация этой стены — лист 84

Визуализация этой стены — лист 84

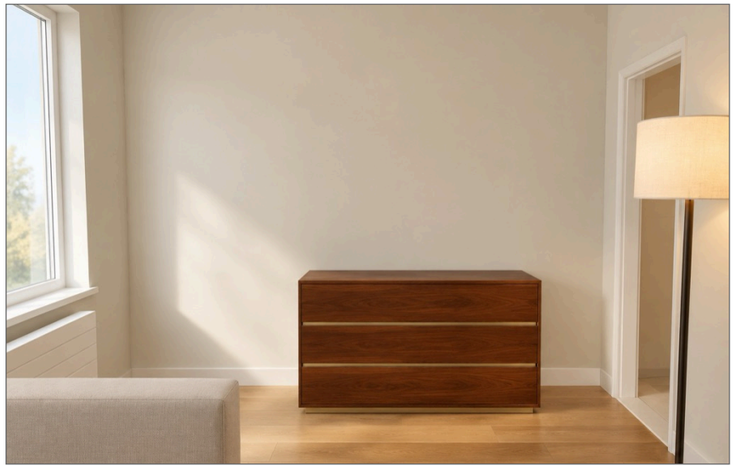

Примечания

1. Размеры — в мм от чистовых поверхностей стен; условные обозначения и общие указания — лист 2.

					Проект: Квартира 103 м²
	Лист	№ док.	Подпись	Дата	Развёртка стены В. Спальня мастер (пом. 10)
Дизайнер	Кырлан А.С.			18.10.26	

Стадия	Лист	Листов
П	88	103

выпуск 18.10.2026 № d119044df4 · стр. 88 из 103

Развёртка стены Г1


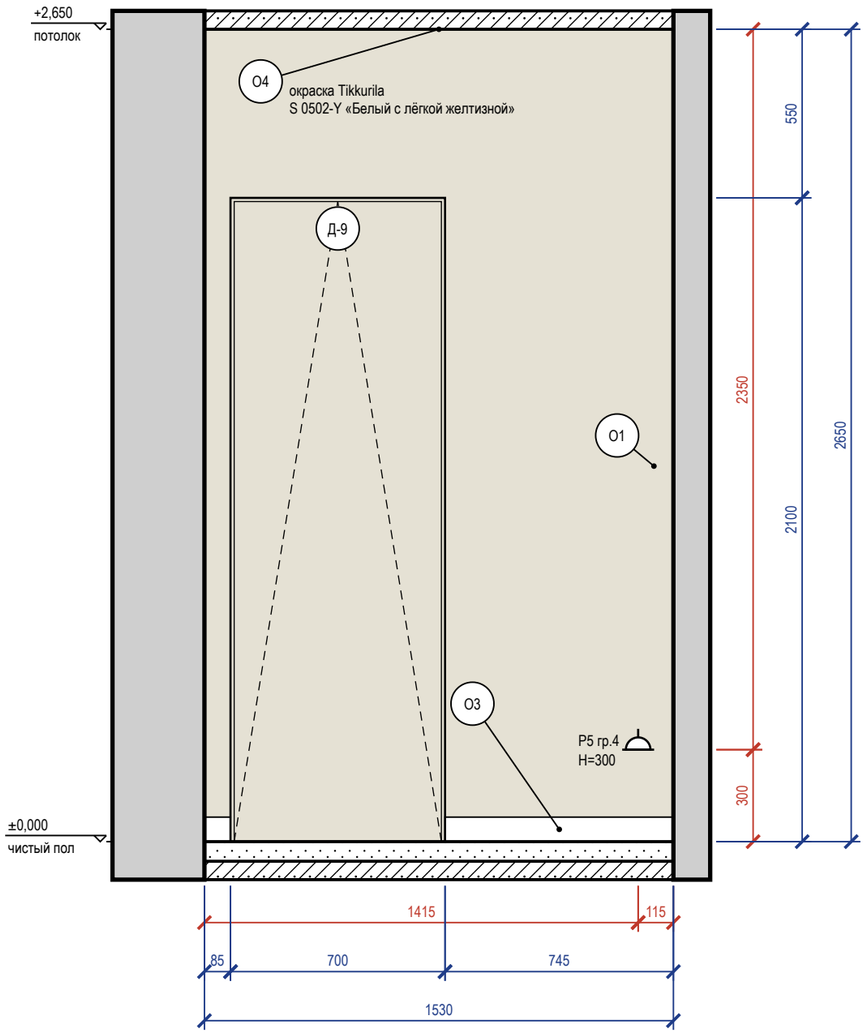


Схема развёрток (М 1:100)

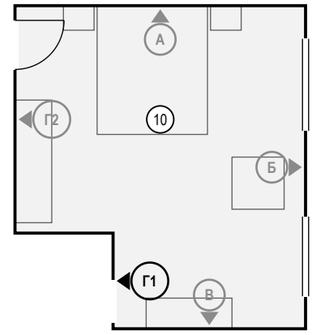

Ведомость отделки (на листе)

Марка	Поверхность	Материал, изделие	Цвет, код	Кол.
О1	стены	окраска, Farrow & Ball Modern Emulsion, матовая, подготовка Q3	Farrow & Ball No. 291 «School House White — тёплый меловой белый»	2,6 м²
О3	плинтус	плинтус МДФ, h 80 мм, аналог: плинтус МДФ под покраску 80×16	Farrow & Ball No. 291 «School House White — тёплый меловой белый»	0,8 м
О4	потолок	окраска, Tikkurila Anti-Reflex 2, глубокоматовая, подготовка Q3	NCS S 0502-Y «Белый с лёгкой желтизной»	22,5 м²

Примечания

1. Размеры — в мм от чистовых поверхностей стен; условные обозначения и общие указания — лист 2.
2. Двери скрытого монтажа — полотно в плоскости стены, отделка стены по полотну, плинтус прерывается у короба (узел — на листе узлов).

					Проект: Квартира 103 м²
	Лист	№ док.	Подпись	Дата	Развёртка стены Г1. Спальня мастер (пом. 10)
Дизайнер	Кырлан А.С.			18.10.26	

Стадия	Лист	Листов
П	89	103

выпуск 18.10.2026 № d119044df4 · стр. 89 из 103

Развёртка стены Г2


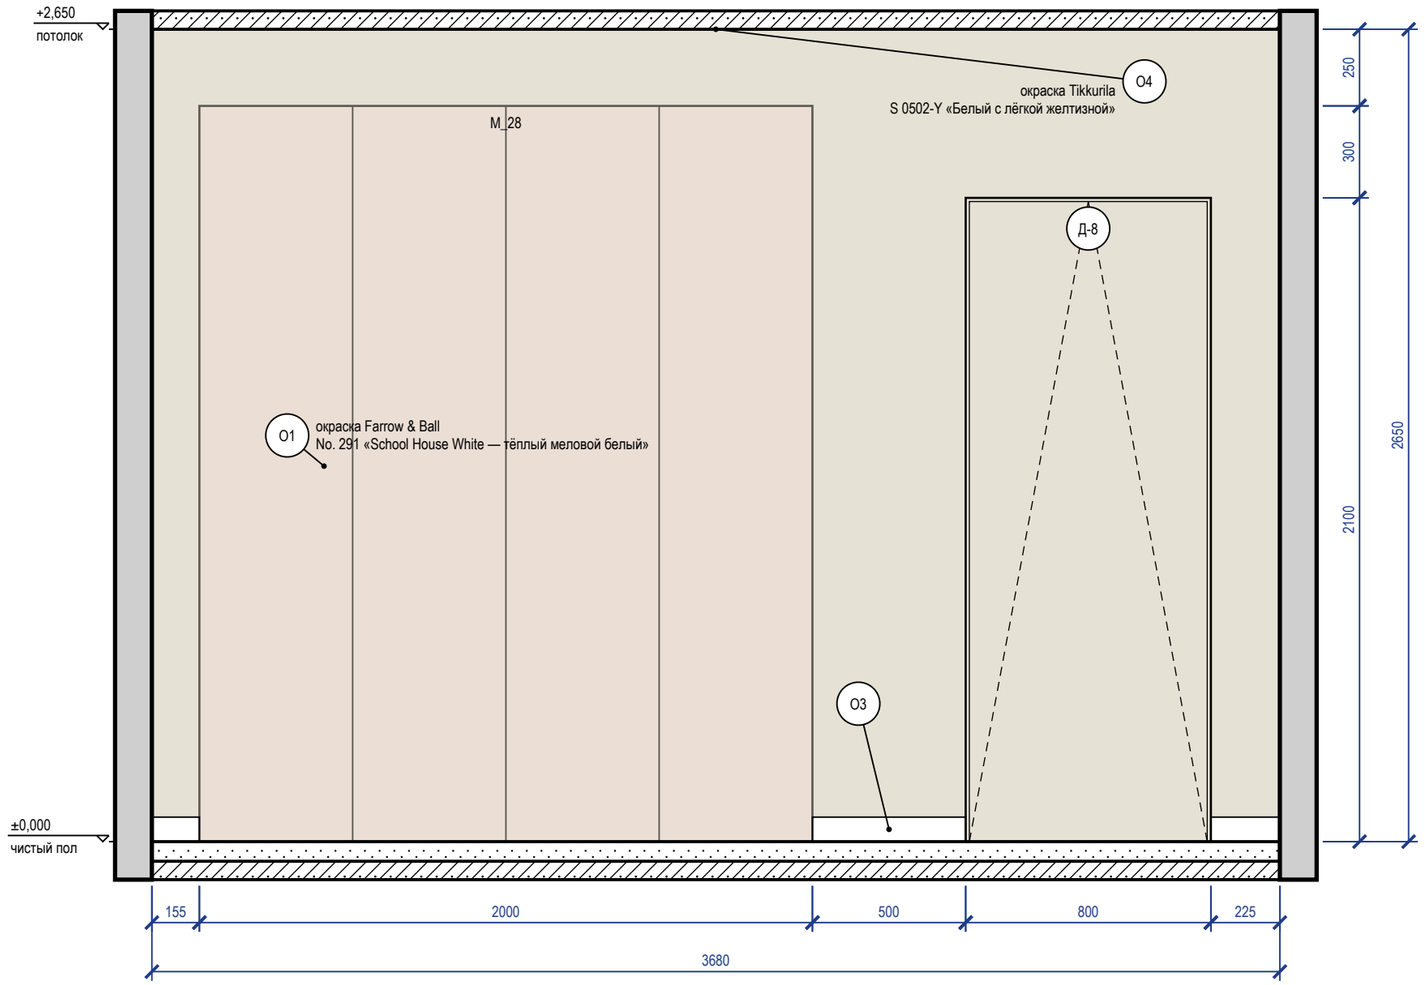


Схема развёрток (М 1:100)

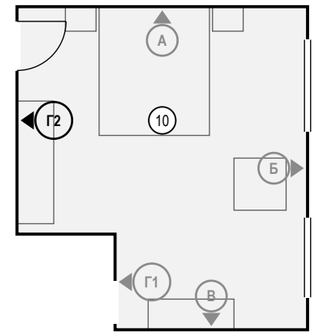

Ведомость отделки (на листе)

Марка	Поверхность	Материал, изделие	Цвет, код	Кол.
О1	стены	окраска, Farrow & Ball Modern Emulsion, матовая, подготовка Q3	Farrow & Ball No. 291 «School House White — тёплый меловой белый»	8,1 м²
О3	плинтус	плинтус МДФ, h 80 мм, аналог: плинтус МДФ под покраску 80×16	Farrow & Ball No. 291 «School House White — тёплый меловой белый»	0,9 м
О4	потолок	окраска, Tikkurila Anti-Reflex 2, глубокоматовая, подготовка Q3	NCS S 0502-Y «Белый с лёгкой желтизной»	22,5 м²

Визуализация этой стены — лист 85



Примечания

1. Размеры — в мм от чистовых поверхностей стен; условные обозначения и общие указания — лист 2.
2. Двери скрытого монтажа — полотно в плоскости стены, отделка стены по полотну, плинтус прерывается у короба (узел — на листе узлов).

	Лист	№ док.	Подпись	Дата
Дизайнер	Кырлан А.С.			18.10.26

Проект: Квартира 103 м²

Развёртка стены Г2. Спальня мастер (пом. 10)

Стадия	Лист	Листов
П	90	103

выпуск 18.10.2026 № d119044df4 · стр. 90 из 103




					Проект: Квартира 103 м²
	Лист	№ док.	Подпись	Дата	
Дизайнер	Кырлан А.С.			18.10.26	Визуализация: Ванная мастер

Стадия	Лист	Листов
П	91	103

выпуск 18.10.2026 № d119044df4 · стр. 91 из 103

Развёртка стены А

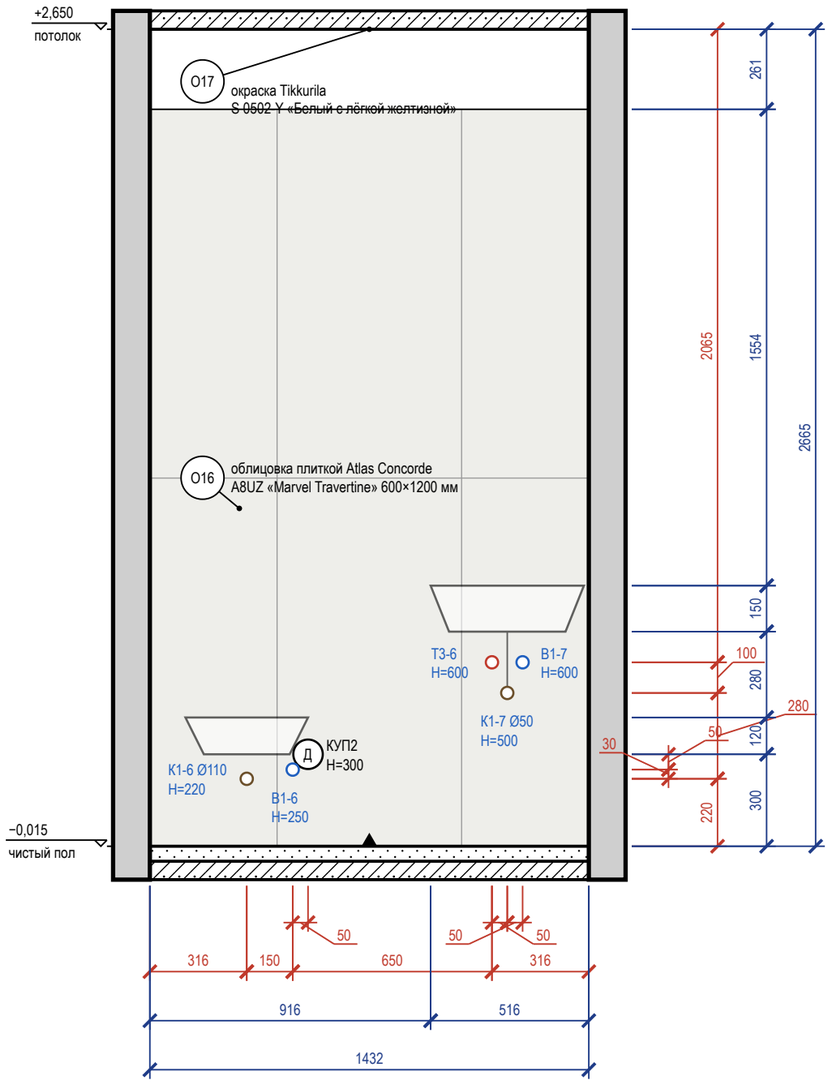

Развёртка стены Б


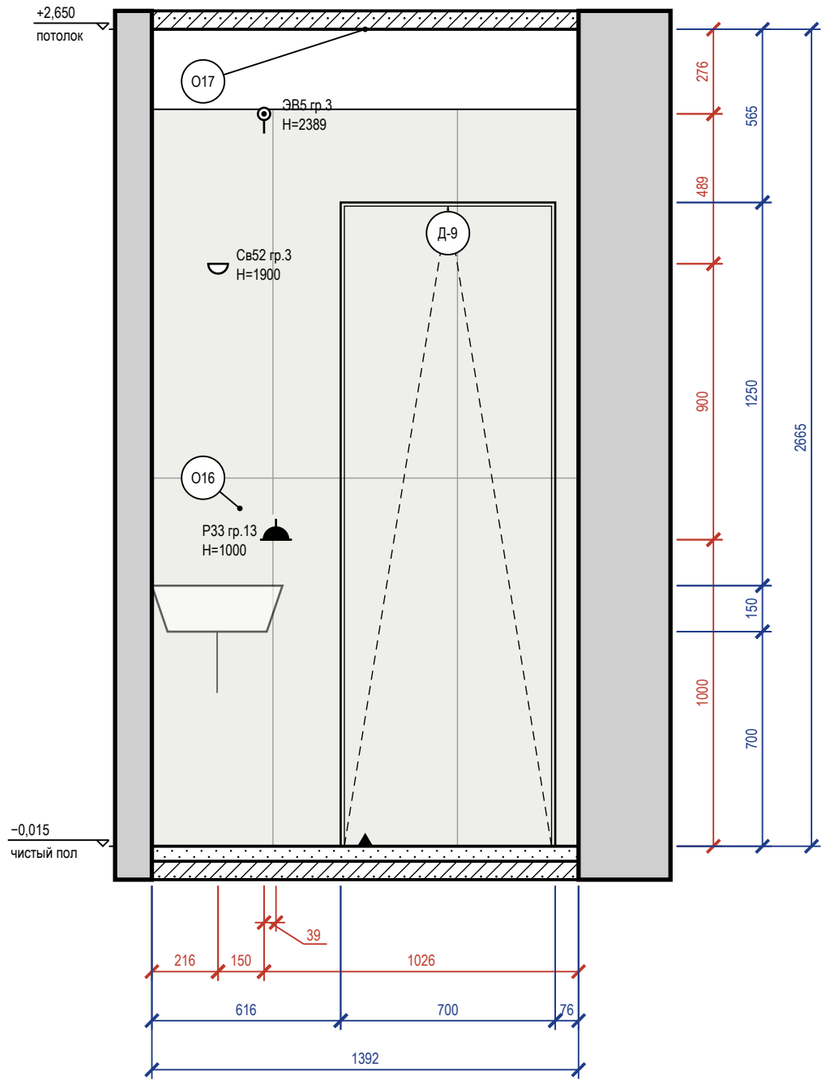


Схема развёрток (М 1:100)

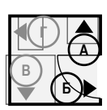

Ведомость отделки (на листе)

Марка	Поверхность	Материал, изделие	Цвет, код	Кол.
О16	стены	облицовка плиткой, Atlas Concorde Marvel Travertine, 600×1200×9 мм, A8UZ, затирка CG2WA	Atlas Concorde A8UZ «Marvel Travertine»	5,3 м²
О17	потолок	окраска, Tikkurila Luja 7, матовая, подготовка Q3	NCS S 0502-Y «Белый с лёгкой желтизной»	2,1 м²

Примечания

1. Размеры — в мм от чистовых поверхностей стен; условные обозначения и общие указания — лист 2.
2. Схема мебели, приборов и декора не является технической документацией для производства мебели; габариты — по паспортам изделий.
3. Выводы ВК — коды и высоты по листу выводов сантехники.
4. Облицовка — по сетке швов 2 мм, раскладка от оси стены (треугольник у пола), целые ряды от пола; подрезки — по листу раскладки плитки.
5. Гидроизоляция в 2 слоя, заход на стены 200 мм — до облицовки, с актом скрытых работ и тестом проливом (узел — на листе узлов).
6. Двери скрытого монтажа — полотно в плоскости стены, отделка стены по полотну, плинтус прерывается у короба (узел — на листе узлов).
7. Линии узора (швы плитки, складки штор, рёбра радиаторов) прерываются у знаков и выносок — просвет между линиями не менее 0,7 мм.

	Лист	№ док.	Подпись	Дата
Дизайнер	Кырлан А.С.			18.10.26


Проект: Квартира 103 м²

Развёртки стен А, Б. Ванная мастер (пом. 11)

Стадия	Лист	Листов
П	92	103

выпуск 18.10.2026 № d119044df4 · стр. 92 из 103

Развёртка стены В

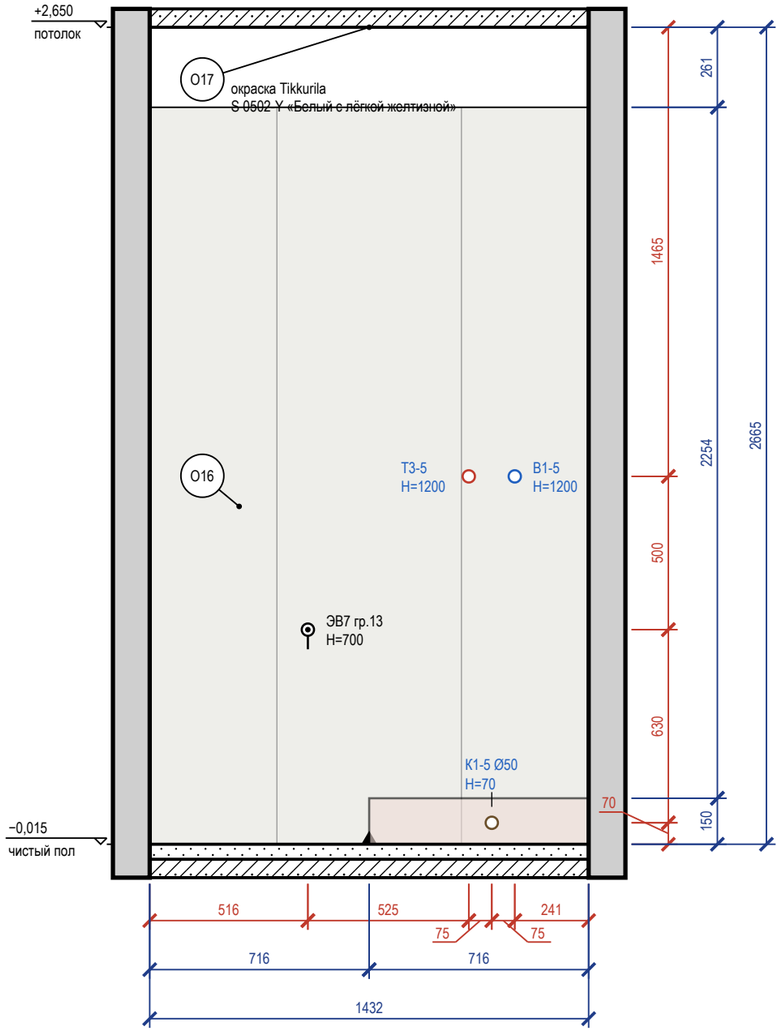

Развёртка стены Г


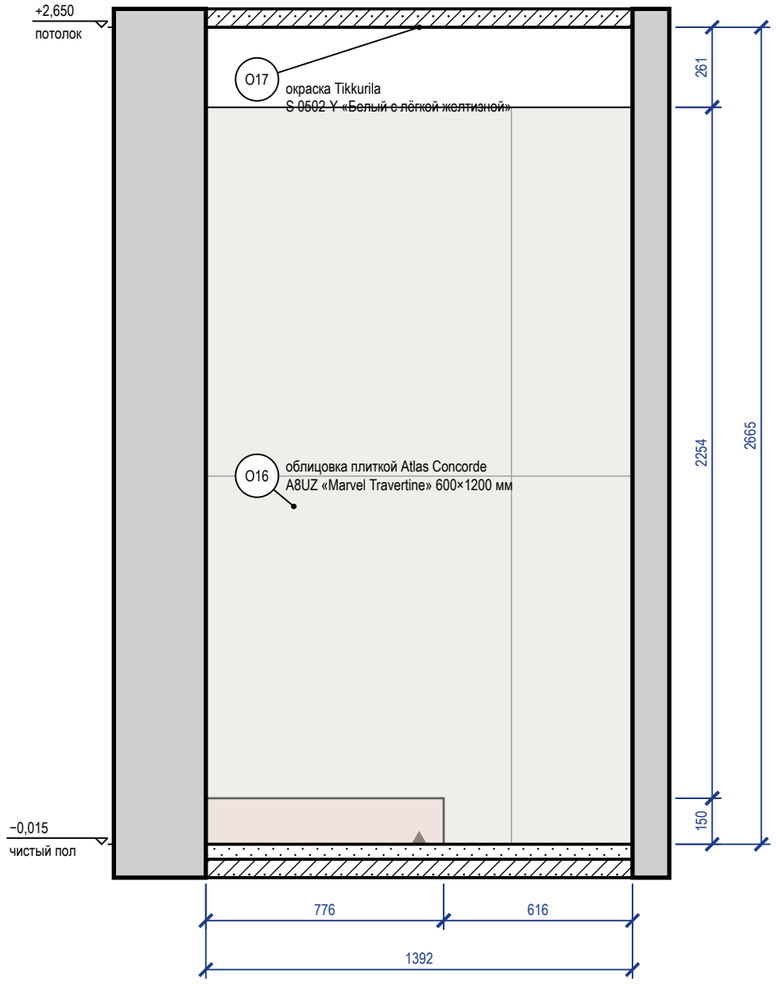


Схема развёрток (М 1:100)

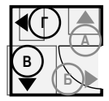

Ведомость отделки (на листе)

Марка	Поверхность	Материал, изделие	Цвет, код	Кол.
О16	стены	облицовка плиткой, Atlas Concorde Marvel Travertine, 600×1200×9 мм, A8UZ, затирка CG2WA	Atlas Concorde A8UZ «Marvel Travertine»	6,8 м²
О17	потолок	окраска, Tikkurila Luja 7, матовая, подготовка Q3	NCS S 0502-Y «Белый с лёгкой желтизной»	2,1 м²

Визуализация этой стены — лист 91



Примечания


1. Размеры — в мм от чистовых поверхностей стен; условные обозначения и общие указания — лист 2.
2. Схема мебели, приборов и декора не является технической документацией для производства мебели; габариты — по паспортам изделий.
3. Выводы ВК — коды и высоты по листу выводов сантехники.
4. Облицовка — по сетке швов 2 мм, раскладка от оси стены (треугольник у пола), целые ряды от пола; подрезки — по листу раскладки плитки.
5. Гидроизоляция в 2 слоя, заход на стены 200 мм — до облицовки, с актом скрытых работ и тестом проливом (узел — на листе узлов).

					Проект: Квартира 103 м²
	Лист	№ док.	Подпись	Дата	Развёртки стен В, Г. Ванная мастер (пом. 11)
Дизайнер	Кырлан А.С.			18.10.26	


Стадия	Лист	Листов
П	93	103

выпуск 18.10.2026 № d119044df4 · стр. 93 из 103


Общий вид

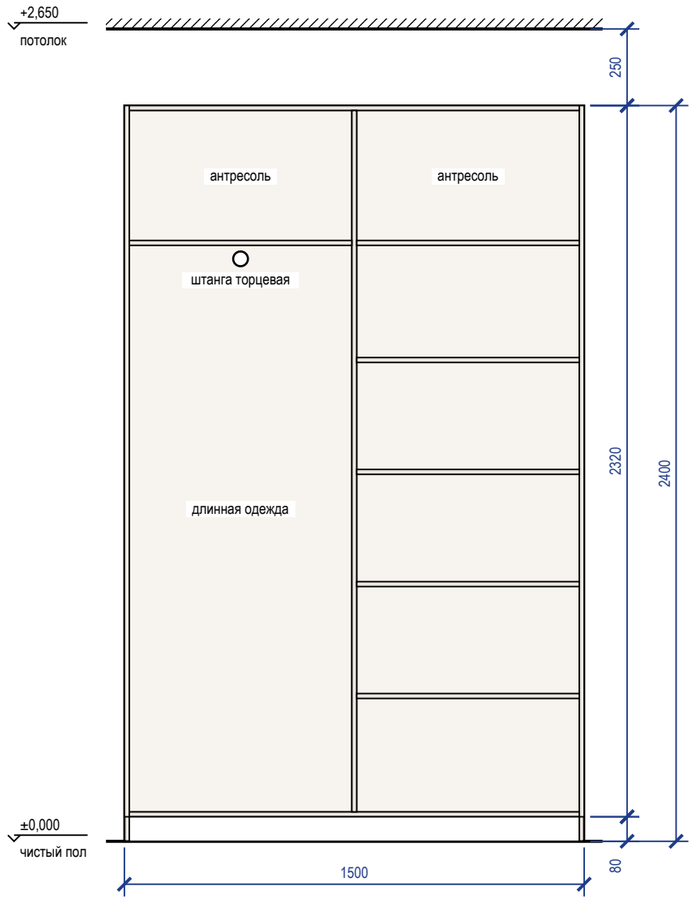


Наполнение, размеры в свету

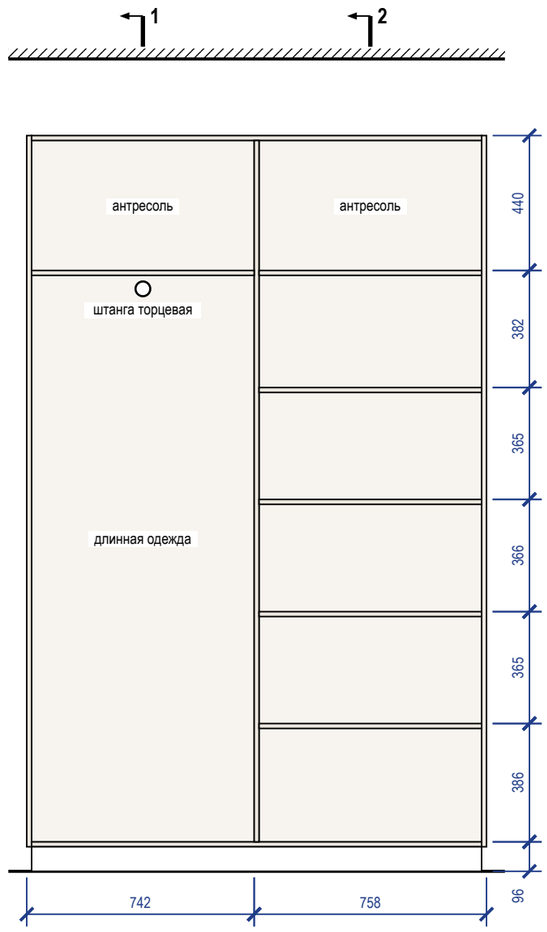

Разрез 1-1

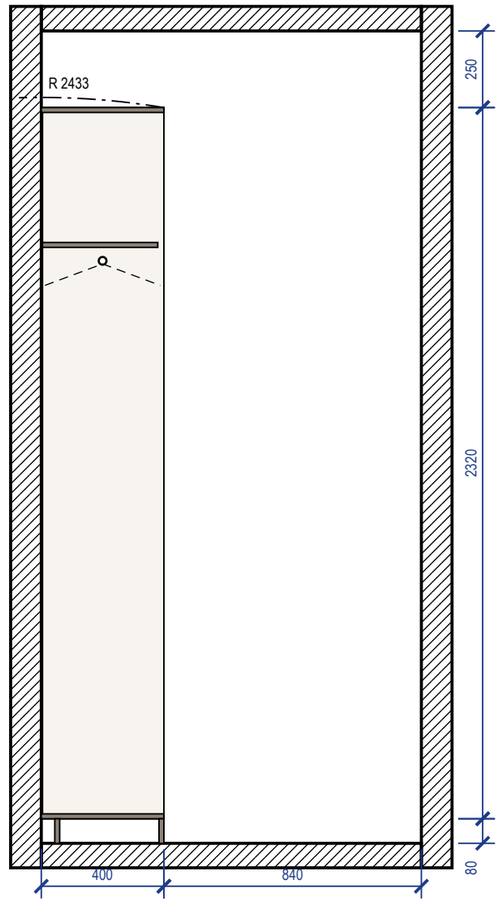


Разрез 2-2

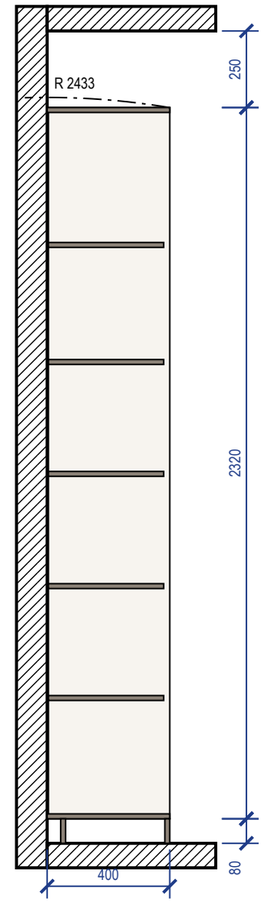

Примечания

1. Размеры — в мм по чистовой отделке; изделие 1500×400×2400 (Ш×Г×В). Перед раскроем — контрольный замер цеха после чистовой отделки стен, пола и потолка.
2. Корпус — ЛДСП 16 мм, задняя стенка ХДФ 4 мм в паз, цоколь 80 мм на регулируемых опорах; открытая система без фасадов, ящики с фасадами.
3. Кромка: скрытые торцы 0,4 мм, видимые 2 мм (ПВХ/АБС).
4. Номинальные зазоры: между фасадами ящиков 3 мм, фасад ящика — стойка 2 мм.
5. Ящики — направляющие полного выдвижения NL 350 (внутренняя глубина 396 мм ≥ NL + 3); присадка по 32-й системе — выполняет цех.
6. Зазор до потолка 250 мм.
7. Подъём корпуса: диагональ боковины $\sqrt{(2400^2 + 400^2)} = 2433$ мм < 2650 мм до потолка — корпус собирается лёжа и поднимается поворотом.
8. Крепление к стене от опрокидывания — уголки 2 шт. к несущему основанию (монтажная схема шкафов).
9. Проход перед изделием 840 мм показан на разрезе 1-1.

3D орто

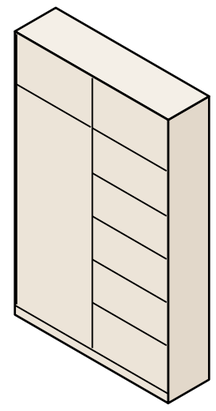


					Проект: Квартира 103 м²
	Лист	№ док.	Подпись	Дата	
Дизайнер	Кырлан А.С.			18.10.26	Система хранения M_05


Стадия	Лист	Листов
П	Д_1	103

выпуск 18.10.2026 № d119044df4 · стр. 94 из 103


Вид с фасадами

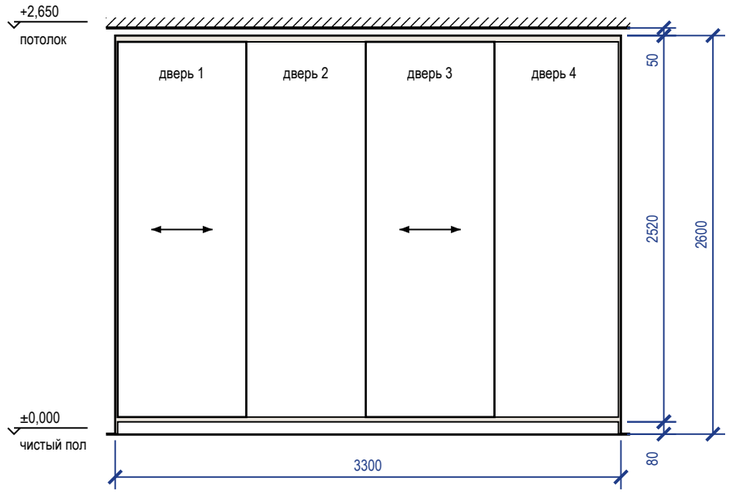


Вид без фасадов

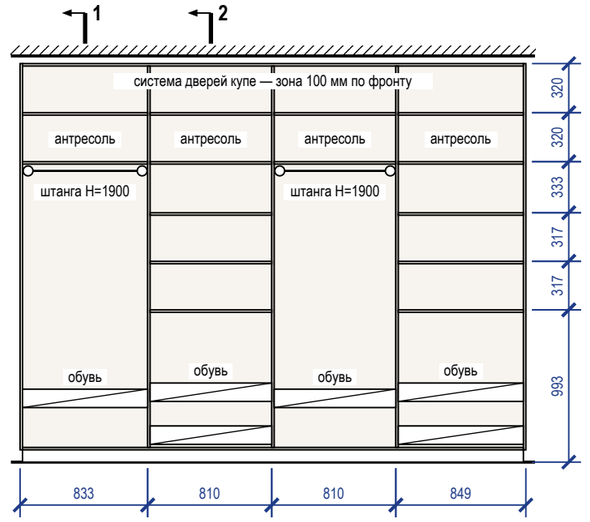

Разрез 1-1

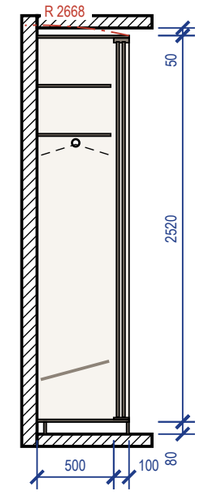


Разрез 2-2

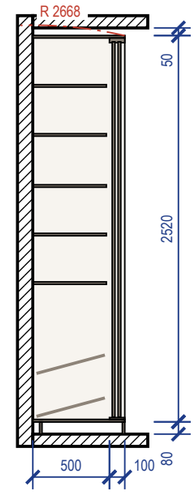

Примечания

1. Размеры — в мм по чистовой отделке; изделие 3300×600×2600 (Ш×Г×В). Перед раскроем — контрольный замер цеха после чистовой отделки стен, пола и потолка.
2. Корпус — ЛДСП 16 мм, задняя стенка ХДФ 4 мм в паз, цоколь 80 мм на регулируемых опорах; двери купе — ЛДСП 10 мм в алюминиевом профиле, нахлёст 30 мм, ширина двери 840 мм, высота — проём минус 40 мм; цвет — по колерной карте.
3. Кромка: скрытые торцы 0,4 мм, видимые 2 мм (ПВХ/АБС).
4. Номинальные зазоры: дверь купе — боковина 3 мм, фасад ящика — стойка 2 мм; ящики внутри купе — с накладкой 30 мм на стойке со стороны нахлёста дверей.
5. Ящики — направляющие полного выдвижения NL 450 (внутренняя глубина 496 мм ≥ NL + 3); присадка по 32-й системе — выполняет цех.
6. Зазор до потолка 50 мм — закрыть планкой в цвет корпуса при монтаже.
7. Подъём корпуса (траектория на виде — красная: корпус не проходит под потолком): диагональ боковины $\sqrt{(2600^2 + 600^2)} = 2668$ мм > 2650 мм до потолка — поднять собранный корпус нельзя: высота корпуса не более 2570 мм, остальное — компенсатор, либо сборка стоя на месте.
8. Крепление к стене от опрокидывания — уголки 2 шт. к несущему основанию (монтажная схема шкафов).


3D орто

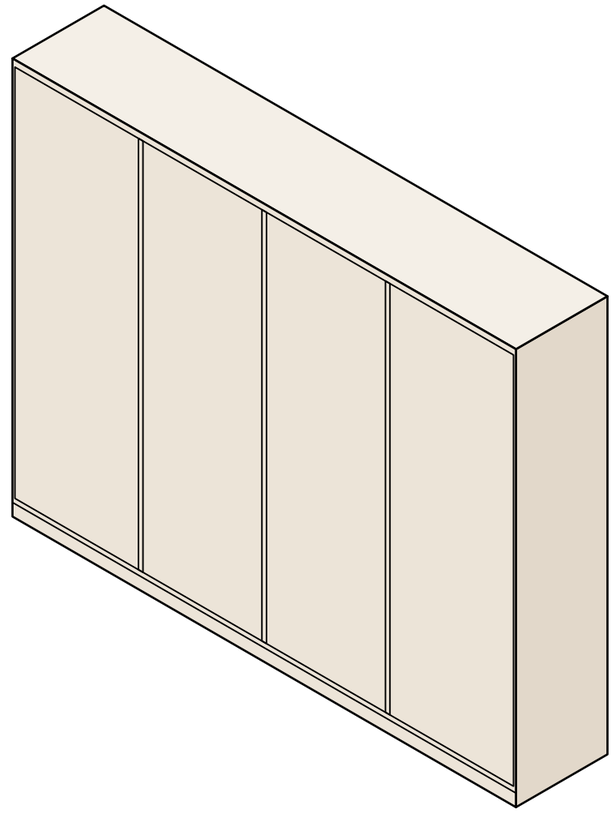


					Проект: Квартира 103 м²
	Лист	№ док.	Подпись	Дата	
Дизайнер	Кырлан А.С.			18.10.26	Шкаф-купе M_11

Стадия	Лист	Листов
П	Д_2	103


Общий вид

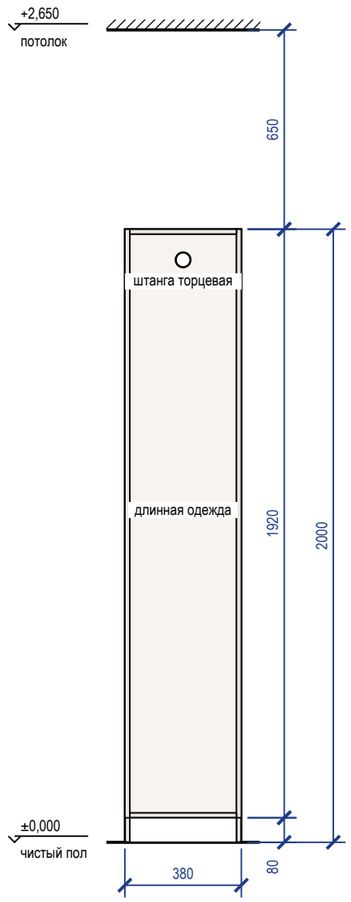

Наполнение, размеры в свету

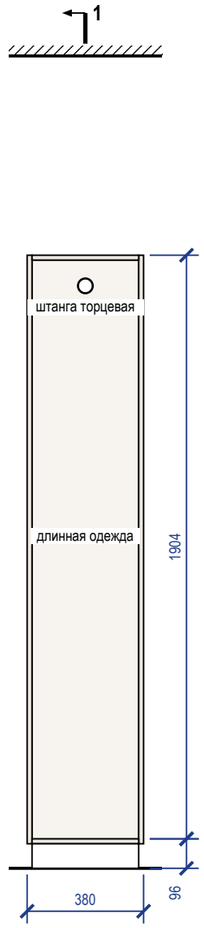


Разрез 1-1

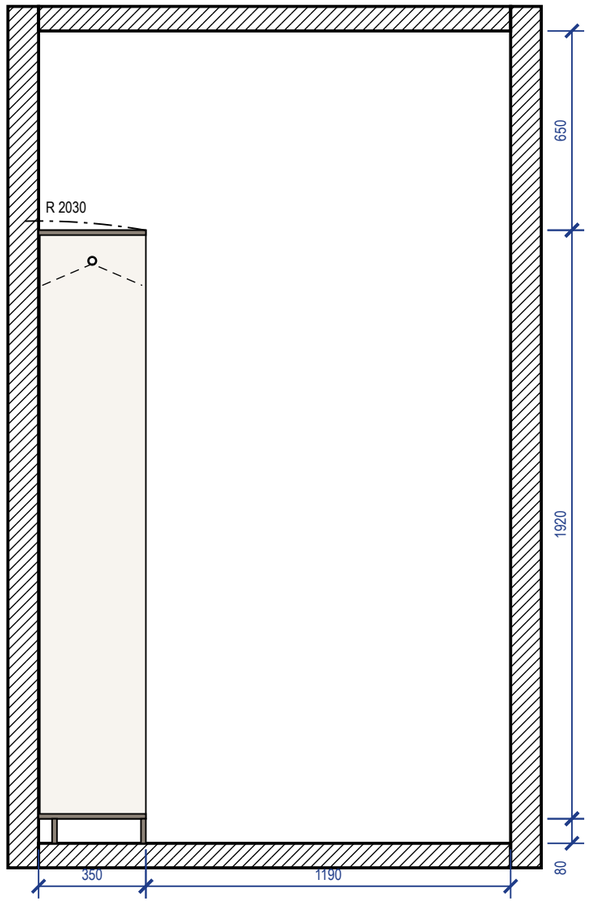

Примечания

1. Размеры — в мм по чистовой отделке; изделие 380×350×2000 (Ш×Г×В). Перед раскроем — контрольный замер цеха после чистовой отделки стен, пола и потолка.
2. Корпус — ЛДСП 16 мм, задняя стенка ХДФ 4 мм в паз, цоколь 80 мм на регулируемых опорах; открытая система без фасадов, ящики с фасадами.
3. Кромка: скрытые торцы 0,4 мм, видимые 2 мм (ПВХ/АБС).
4. Номинальные зазоры: между фасадами ящиков 3 мм, фасад ящика — стойка 2 мм.
5. Ящики — направляющие полного выдвижения NL 300 (внутренняя глубина 346 мм ≥ NL + 3); присадка по 32-й системе — выполняет цех.
6. Зазор до потолка 650 мм.
7. Подъём корпуса: диагональ боковины $\sqrt{(2000^2 + 350^2)} = 2030$ мм < 2650 мм до потолка — корпус собирается лёжа и поднимается поворотом.
8. Крепление к стене от опрокидывания — уголки 2 шт. к несущему основанию (монтажная схема шкафов).
9. Проход перед изделием 1190 мм показан на разрезе 1-1.

3D орто

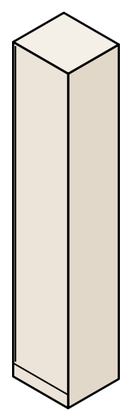


					Проект: Квартира 103 м²
	Лист	№ док.	Подпись	Дата	
Дизайнер	Кырлан А.С.			18.10.26	Система хранения M_21


Стадия	Лист	Листов
П	Д_3	103

выпуск 18.10.2026 № d119044df4 · стр. 96 из 103


Вид с фасадами

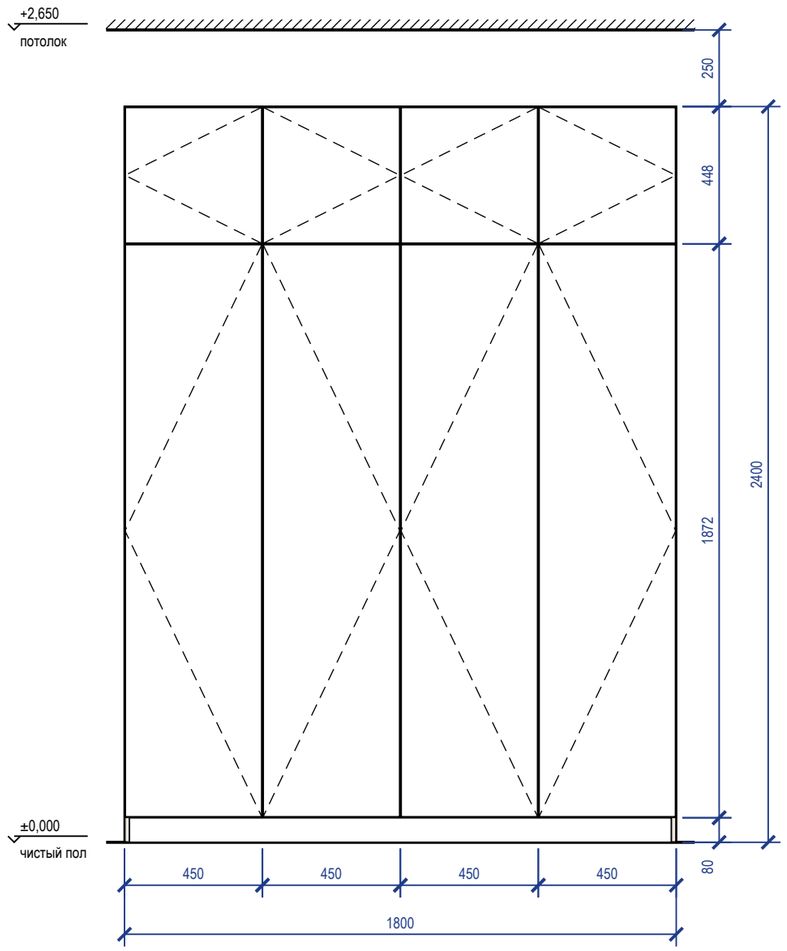


Вид без фасадов

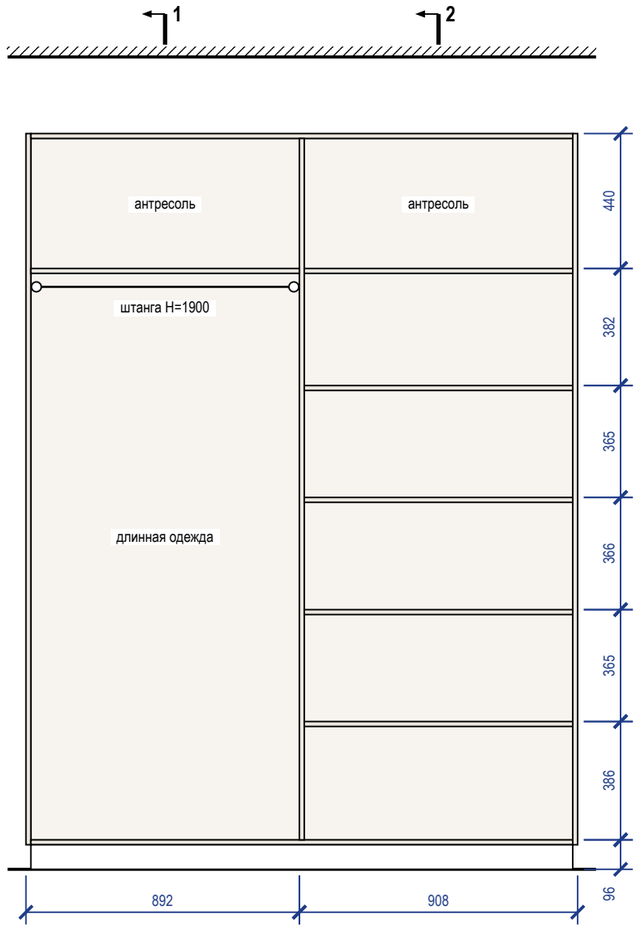

Разрез 1-1

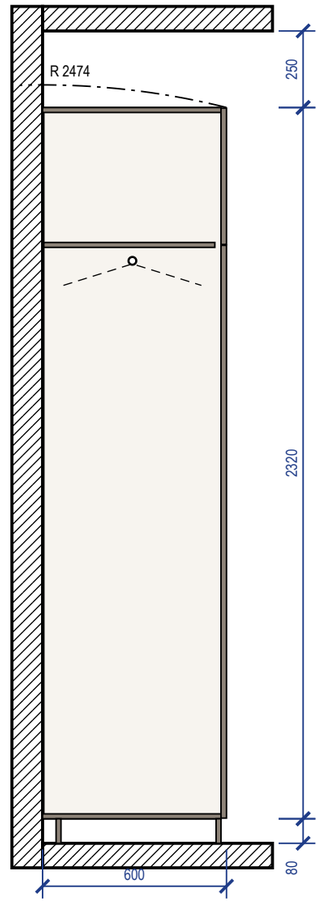


Разрез 2-2

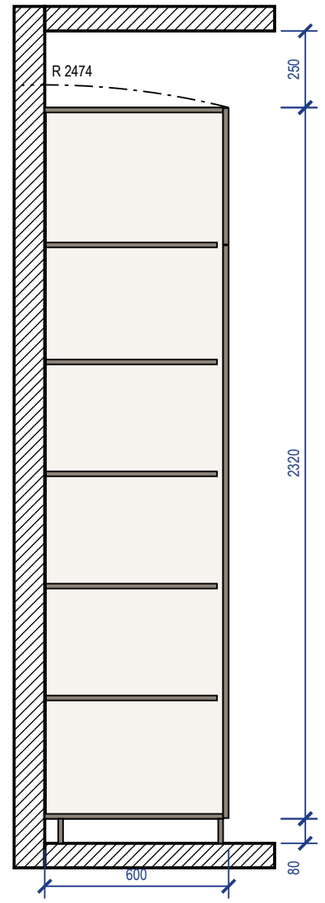

Примечания

1. Размеры — в мм по чистовой отделке; изделие 1800×600×2400 (Ш×Г×В). Перед раскроем — контрольный замер цеха после чистовой отделки стен, пола и потолка.
2. Корпус — ЛДСП 16 мм, задняя стенка ХДФ 4 мм в паз, цоколь 80 мм на регулируемых опорах; фасады — МДФ, эмаль матовая 18 мм накладные, цвет — по колерной карте; петли с доводчиком: фасад 1869 мм — 4 петли, фасад 445 мм — 2 петли.
3. Кромка: скрытые торцы 0,4 мм, видимые 2 мм (ПВХ/АБС).
4. Номинальные зазоры: между фасадами 3 мм, фасад — стена и фасад — потолок не менее 3 мм, фасад ящика — стойка 2 мм.
5. Ящики — направляющие полного выдвижения NL 550 (внутренняя глубина 578 мм ≥ NL + 3); присадка по 32-й системе — выполняет цех.
6. Зазор до потолка 250 мм.
7. Подъём корпуса: диагональ боковины $\sqrt{(2400^2 + 600^2)} = 2474$ мм < 2650 мм до потолка — корпус собирается лёжа и поднимается поворотом.
8. Крепление к стене от опрокидывания — уголки 2 шт. к несущему основанию (монтажная схема шкафов).


3D орто

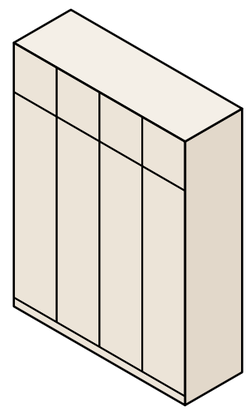


					Проект: Квартира 103 м²	
	Лист	№ док.	Подпись	Дата		
Дизайнер	Кырлан А.С.			18.10.26	Шкаф распашной М_23	Стадия: П; Лист: Д_4; Листов: 103

выпуск 18.10.2026 № d119044df4 · стр. 97 из 103


Вид с фасадами

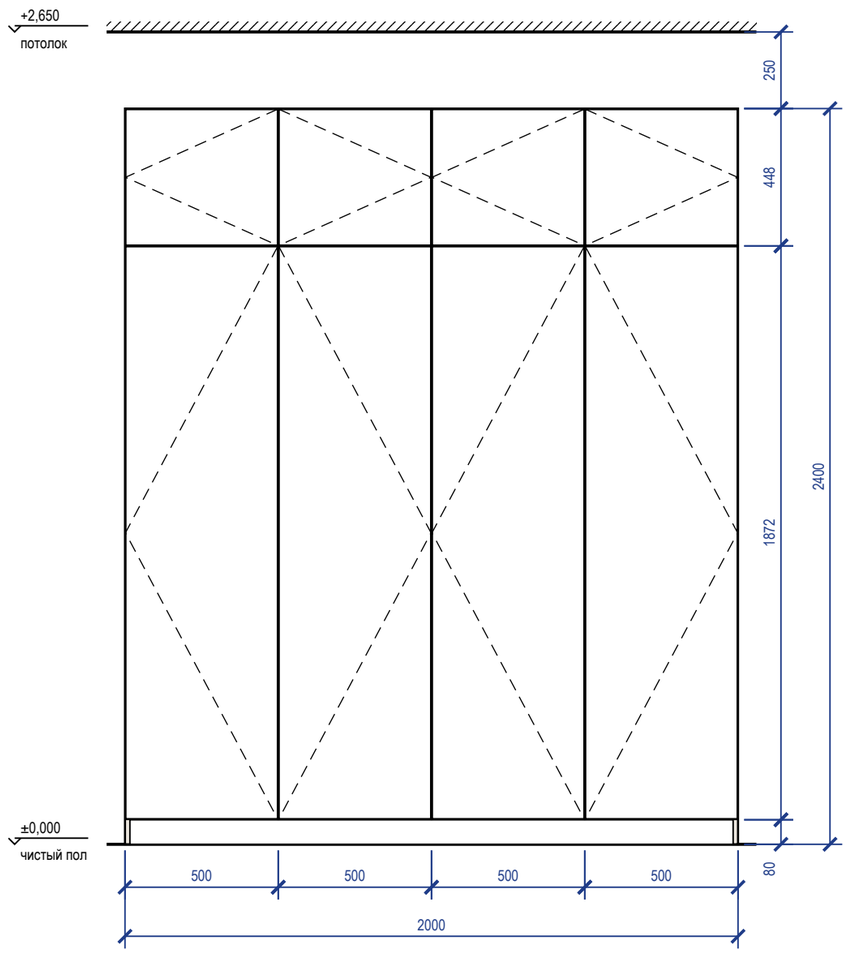


Вид без фасадов

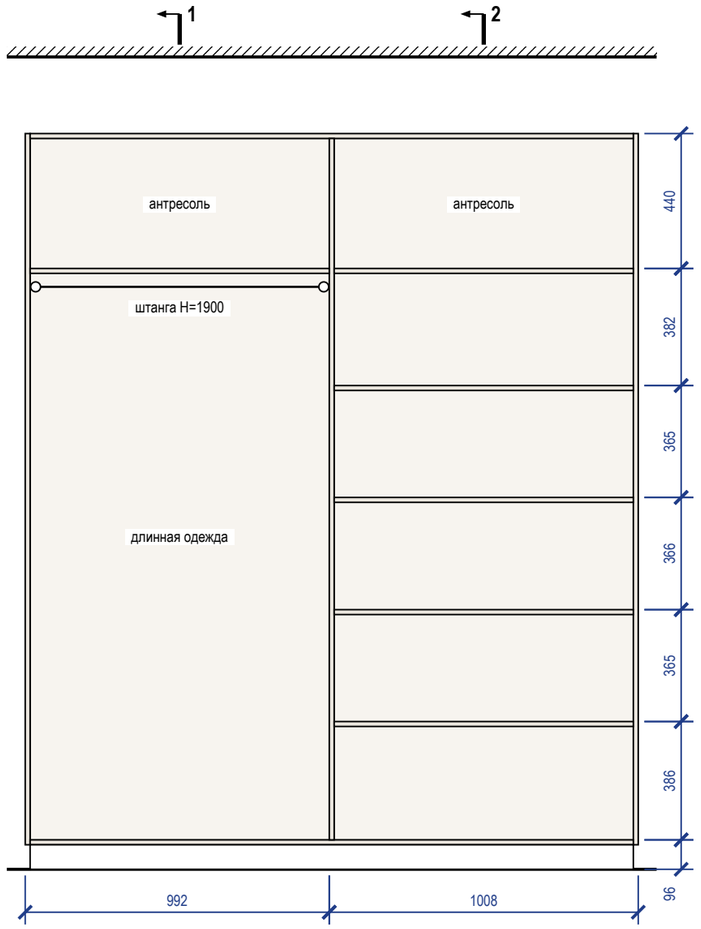

Разрез 1-1

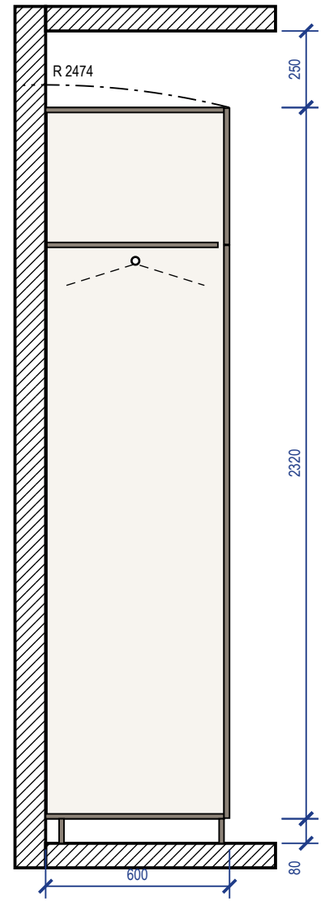


Разрез 2-2

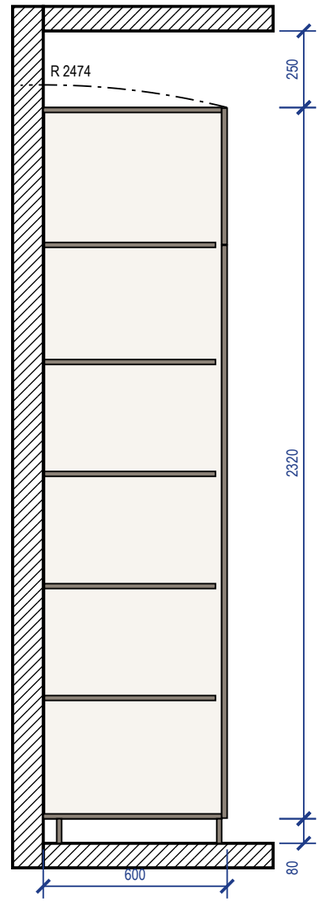

Примечания

1. Размеры — в мм по чистовой отделке; изделие 2000×600×2400 (Ш×Г×В). Перед раскроем — контрольный замер цеха после чистовой отделки стен, пола и потолка.
2. Корпус — ЛДСП 16 мм, задняя стенка ХДФ 4 мм в паз, цоколь 80 мм на регулируемых опорах; фасады — МДФ, эмаль матовая 18 мм накладные, цвет — по колерной карте; петли с доводчиком: фасад 1869 мм — 4 петли, фасад 445 мм — 2 петли.
3. Кромка: скрытые торцы 0,4 мм, видимые 2 мм (ПВХ/АБС).
4. Номинальные зазоры: между фасадами 3 мм, фасад — стена и фасад — потолок не менее 3 мм, фасад ящика — стойка 2 мм.
5. Ящики — направляющие полного выдвижения NL 550 (внутренняя глубина 578 мм ≥ NL + 3); присадка по 32-й системе — выполняет цех.
6. Зазор до потолка 250 мм.
7. Подъём корпуса: диагональ боковины $\sqrt{(2400^2 + 600^2)} = 2474$ мм < 2650 мм до потолка — корпус собирается лёжа и поднимается поворотом.
8. Крепление к стене от опрокидывания — уголки 2 шт. к несущему основанию (монтажная схема шкафов).


3D орто

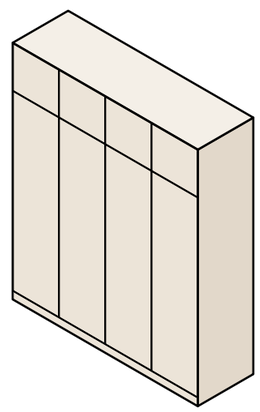


					Проект: Квартира 103 м²		
	Лист	№ док.	Подпись	Дата	Шкаф распашной М_28	Стадия	Лист	Листов
Дизайнер	Кырлан А.С.			18.10.26		П	Д_5	103

выпуск 18.10.2026 № d1190444df4 · стр. 98 из 103


Вид с фасадами

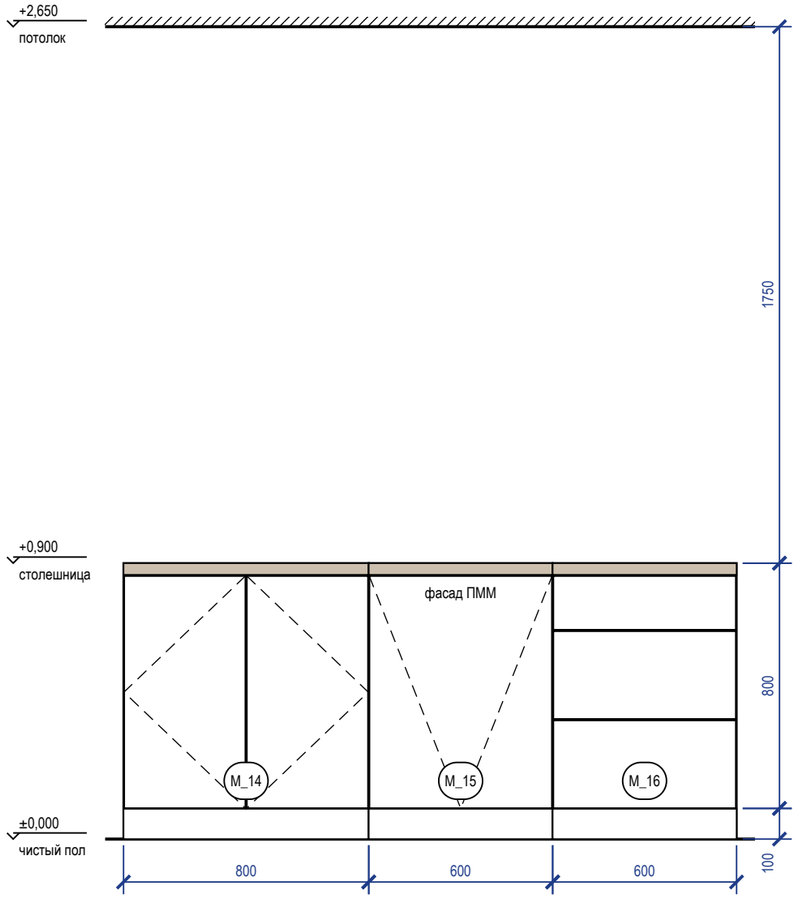


Вид без фасадов (наполнение, выводы)

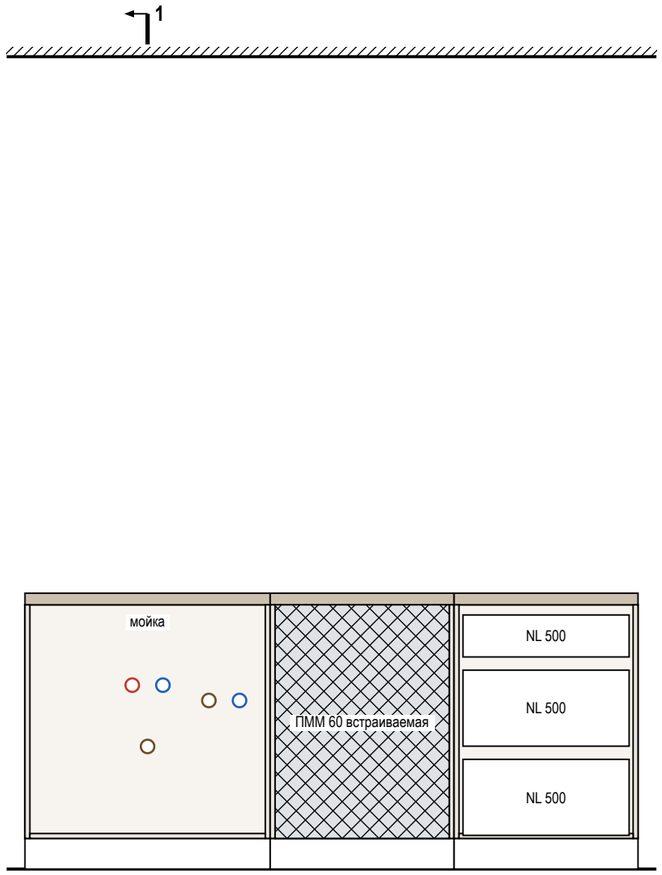

Разрез 1-1

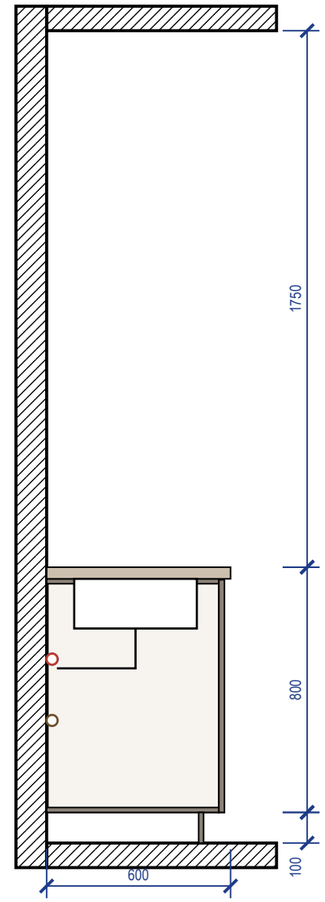

3D орто

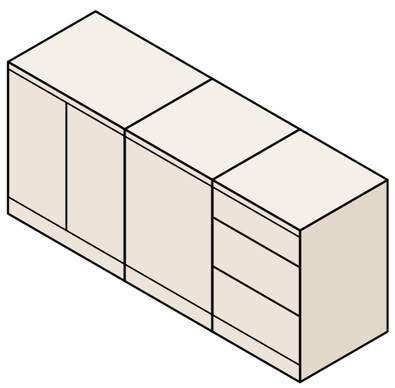

Примечания


1. Размеры — в мм по чистовой отделке, вид из помещения; марки — как на плане расстановки. Перед раскроем — контрольный замер цеха после фартука и пола.
2. Корпуса — ЛДСП 16 мм, задняя стенка ХДФ 4 мм; фасады — МДФ, эмаль матовая 18 мм, цвет по колерной карте; столешница 38 мм, свес 20 мм; цоколь 100 мм.
3. Кромка: скрытые торцы 0,4 мм, видимые 2 мм. Номинальные зазоры: между фасадами 3 мм, фасад — столешница 3 мм, фасад — стена не менее 3 мм.
4. Ящики полного выдвижения и петли — с доводчиком; присадка по 32-й системе — выполняет цех.
5. Ниши техники — по монтажным схемам выбранных моделей: решётка в цоколе и канал за пеналом холодильника, зазор за духовым шкафом, фасад ПММ на двери машины.

					Проект: Квартира 103 м²
	Лист	№ док.	Подпись	Дата	Кухня (пом. 5). Развёртка гарнитура
Дизайнер	Кырлан А.С.			18.10.26	


Стадия	Лист	Листов
П	Д_6	103

выпуск 18.10.2026 № d119044df4 · стр. 99 из 103


Вид с фасадами

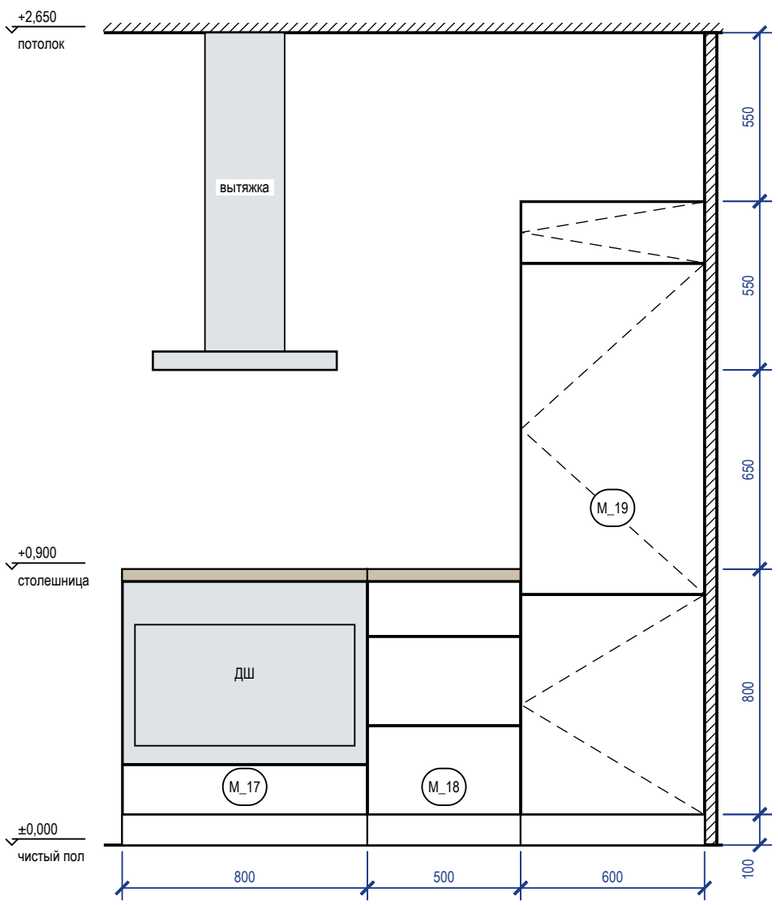


Вид без фасадов (наполнение, выводы)

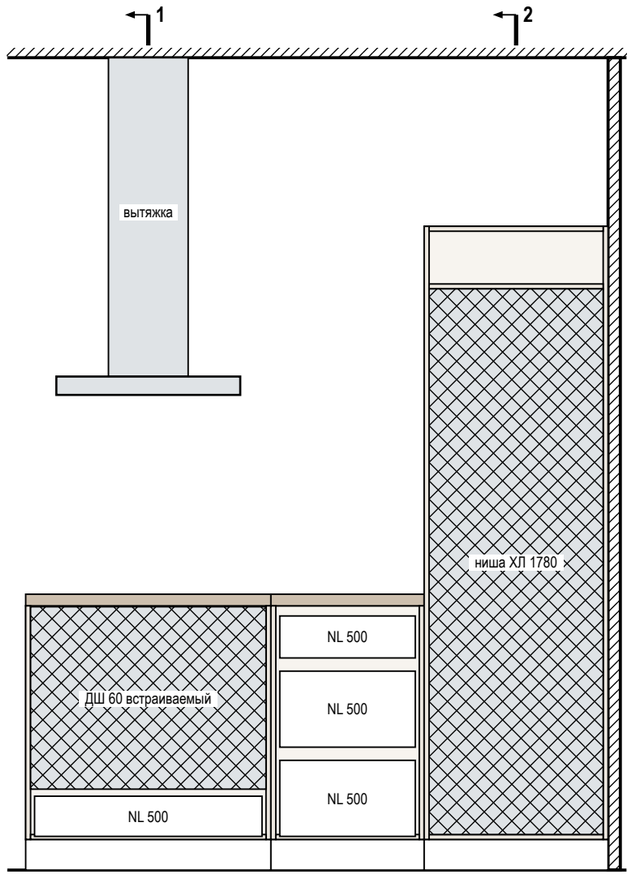


Разрез 1-1

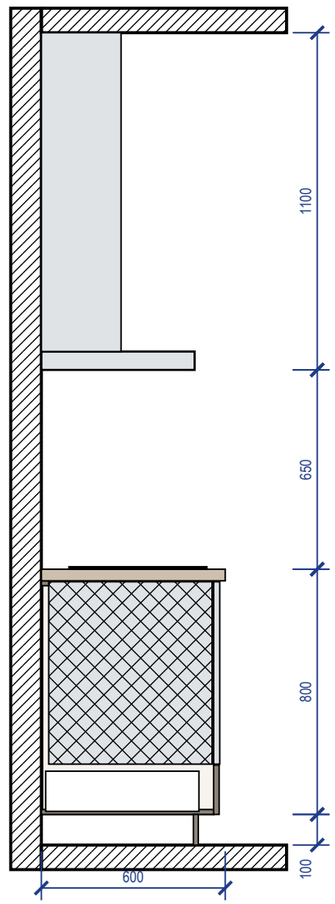

Разрез 2-2

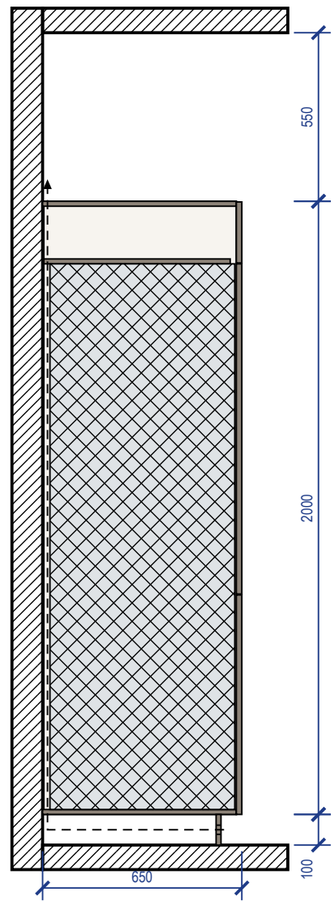

3D орто

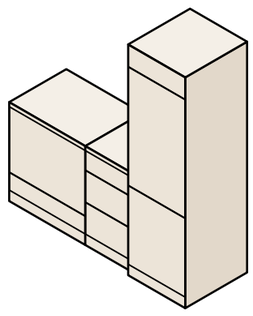

Примечания

1. Размеры — в мм по чистовой отделке, вид из помещения; марки — как на плане расстановки. Перед раскроем — контрольный замер цеха после фартука и пола.
2. Корпуса — ЛДСП 16 мм, задняя стенка ХДФ 4 мм; фасады — МДФ, эмаль матовая 18 мм, цвет по колерной карте; столешница 38 мм, свес 20 мм; цоколь 100 мм.
3. Кромка: скрытые торцы 0,4 мм, видимые 2 мм. Номинальные зазоры: между фасадами 3 мм, фасад — столешница 3 мм, фасад — стена не менее 3 мм.
4. Ящики полного выдвижения и петли — с доводчиком; присадка по 32-й системе — выполняет цех.
5. Низ вытяжки — не ниже 650 мм над варочной панелью или по паспорту модели; короб воздуховода — до потолка.
6. Ниши техники (холодильник — ориентир 1780 мм) — по монтажным схемам выбранных моделей: решётка в цоколе и канал за пеналом холодильника, зазор за духовым шкафом, фасад ПММ на двери машины.

					Проект: Квартира 103 м²		
	Лист	№ док.	Подпись	Дата	Кухня (пом. 5). Развёртка гарнитура	Стадия	Лист	Листов
Дизайнер	Кырлан А.С.			18.10.26		П	Д_7	103

выпуск 18.10.2026 № d119044df4 · стр. 100 из 103

Ведомость отделки помещений (форма 1 прил. А ГОСТ 21.501-2018). Лист 1 из 2

№	Наименование помещения	Потолок			Стены и перегородки			Низ стен (плинтус)			Пол		Примечание
		Вид отделки	Код цвета	S, м²	Вид отделки	Код цвета	S, м²	Вид отделки	Код цвета	L, м	Вид отделки	S, м²	
1	Кабинет-библиотека 10,57 м²	Окраска, Tikkurila Anti-Reflex 2, глубокоматовая, 2 слоя, подготовка Q3	NCS S 0502-Y	10,57	Окраска, Farrow & Ball Modern Emulsion, матовая, 2 слоя, подготовка Q3 Акцент — стена А: окраска, Farrow & Ball Modern Emulsion, матовая, 2 слоя, подготовка Q3	Farrow & Ball No. 291 Farrow & Ball No. 289	20,83 11,87	Плинтус МДФ h=80 мм, аналог: МДФ под покраску 80×16	Farrow & Ball No. 291	12,9	Инженерная доска, 1167-4250, 2100×127 мм, на клею; тип 1, отм. ЧП ±0,000	10,57	Н стен 2650 (до потолка); плинтус в цвет: стены
2	Кладовая 2,93 м²	Окраска, Tikkurila Anti-Reflex 2, глубокоматовая, 2 слоя, подготовка Q3	NCS S 0502-Y	2,93	Окраска, Tikkurila Harmony, матовая, 2 слоя, подготовка Q3	NCS S 0502-Y	17,61	Плинтус МДФ h=80 мм, аналог: МДФ под покраску 80×16	NCS S 0502-Y	6,5	Инженерная доска, 1167-4250, 2100×127 мм, на клею; тип 1, отм. ЧП ±0,000	2,93	Н стен 2650 (до потолка); плинтус в цвет: стены
3	Гостиная-столовая 20,32 м²	Окраска, Tikkurila Anti-Reflex 2, глубокоматовая, 2 слоя, подготовка Q3	Farrow & Ball No. 291	20,32	Окраска, Tikkurila Optiva 5 Matt, матовая, 2 слоя, подготовка К3 Акцент — стена А: окраска, Tikkurila Optiva 5 Matt, матовая, 3 слоя, подготовка К3	Farrow & Ball No. 291 Farrow & Ball No. 255	24,85 12,33	Плинтус МДФ h=80 мм, аналог: МДФ под окраску 80×16 мм	Farrow & Ball No. 291	14,7	Инженерная доска, 1167-4250, 2100×127 мм, на клею; тип 2, отм. ЧП ±0,000	20,32	Н стен 2650 (до потолка); колеруется в код стен, но по эмали на МДФ: сличать отдельным выкрасом на своей подложке (выкрас № 10); плинтус в цвет: стены
4	Прихожая-холл 12,91 м²	Окраска, Tikkurila Anti-Reflex 2, глубокоматовая, 2 слоя, подготовка Q3	NCS S 0502-Y	12,91	Окраска, Farrow & Ball Modern Emulsion, матовая, 2 слоя, подготовка Q3	Farrow & Ball No. 291	35,51	Плинтус МДФ h=80 мм, аналог: МДФ под покраску 80×16	Farrow & Ball No. 291	12,6	Керамогранит, A8UZ, 600×1200×9 мм; тип 3, отм. ЧП ±0,000	12,91	Н стен 2650 (до потолка); матовая моющаяся, класс 1 EN 13300 — осознанно вместо полуматовой; плинтус в цвет: стены
5	Кухня 6,52 м²	Окраска, Tikkurila Luja 7, матовая, 2 слоя, подготовка Q3	Farrow & Ball No. 291	6,52	Окраска, Tikkurila Luja 7, полуматовая, 2 слоя, подготовка К3 Фартук кухни (стена Б, В): облицовка керамогранитом, аналог: керамогранит матовый, тон F497, 600×600×9 мм, клей C2 TE S1, затирка CG2WA	Farrow & Ball No. 291 #F1F1EC	21,86 1,68	Плинтус МДФ h=80 мм, аналог: МДФ под окраску 80×16 мм	Farrow & Ball No. 291	9,4	Инженерная доска, 1167-4250, 2100×127 мм, на клею; тип 4, отм. ЧП ±0,000	6,52	Н стен 2650 (до потолка); влагостойкая полуматовая окраска (класс мокрого истирания 1 по EN 13300); категория К3 по СП 71.13330.2017, табл. 7.5; по ГКЛ каркаса П113, влагостойкая окраска; Q3 колеруется в код стен, но по эмали на МДФ: сличать отдельным выкрасом на своей подложке (выкрас № 10); плинтус в цвет: стены
6	Ванная 3,91 м²	Окраска, Tikkurila Luja 7, матовая, 2 слоя, подготовка Q3	NCS S 0502-Y	3,91	Облицовка плиткой, A8UZ, 600×1200×9 мм, клей C2 TE S1, затирка CG2WA	Atlas Concorde A8UZ	18,00	нет			Керамогранит, A8UZ, 600×1200×9 мм; тип 5, отм. ЧП −0,015	3,91	Н стен 2665 (до потолка); гидроизоляция обмазочная, 2 слоя, с заведением на стены 200 мм (по пирогу пола); тест проливом и акт скрытых работ
7	Постирочная 1,51 м²	Окраска, Tikkurila Anti-Reflex 2, глубокоматовая, 2 слоя, подготовка Q3	NCS S 0502-Y	1,51	Окраска, Tikkurila Harmony, матовая, 2 слоя, подготовка Q3	NCS S 0502-Y	11,89	Плинтус МДФ h=80 мм, аналог: МДФ под покраску 80×16	NCS S 0502-Y	4,3	Инженерная доска, 1167-4250, 2100×127 мм, на клею; тип 1, отм. ЧП ±0,000	1,51	Н стен 2650 (до потолка); плинтус в цвет: стены
8	Спальня 2 11,42 м²	Окраска, Tikkurila Anti-Reflex 2, глубокоматовая, 2 слоя, подготовка Q3	NCS S 0502-Y	11,42	Окраска, Farrow & Ball Modern Emulsion, матовая, 2 слоя, подготовка Q3 Акцент — стена А: окраска, Farrow & Ball Modern Emulsion, матовая, 2 слоя, подготовка Q3	Farrow & Ball No. 291 Farrow & Ball No. 289	21,85 12,56	Плинтус МДФ h=80 мм, аналог: МДФ под покраску 80×16	Farrow & Ball No. 291	13,6	Инженерная доска, 1167-4250, 2100×127 мм, на клею; тип 1, отм. ЧП ±0,000	11,42	Н стен 2650 (до потолка); плинтус в цвет: стены
9	Коридор 6,02 м²	Окраска, Tikkurila Anti-Reflex 2, глубокоматовая, 2 слоя, подготовка Q3	NCS S 0502-Y	6,02	Окраска, Farrow & Ball Modern Emulsion, матовая, 2 слоя, подготовка Q3	Farrow & Ball No. 291	30,60	Плинтус МДФ h=80 мм, аналог: МДФ под покраску 80×16	Farrow & Ball No. 291	10,8	Инженерная доска, 1167-4250, 2100×127 мм, на клею; тип 1, отм. ЧП ±0,000	6,02	Н стен 2650 (до потолка); матовая моющаяся, класс 1 EN 13300 — осознанно вместо полуматовой; плинтус в цвет: стены

Примечания

1. Ведомость продолжена на листе 2 из 2; итоги, сводка площадей и примечания — на последнем листе ведомости.

					Проект: Квартира 103 м²
	Лист	№ док.	Подпись	Дата	Ведомость отделки помещений. Лист 1 из 2
Дизайнер	Кырлан А.С.			18.10.26	

Стадия	Лист	Листов
П	С1	103


выпуск 18.10.2026 № d119044df4 · стр. 101 из 103

Поз.	Наименование и техническая характеристика	Тип, марка, обозначение документа	Код продукции	Поставщик	Ед. изм.	Кол.	Образец	Примечание
	Лакокрасочные материалы							
1	Краска интерьерная водно-дисперсионная акриловая для стен, матовая, класс мокрого истирания 1 по EN 13300, база A; цвет Farrow & Ball No. 291 «School House White — тёплый меловой белый», колеровка машинная	Farrow & Ball Modern Emulsion		Farrow & Ball	л	40		поз. К1 колерной карты; пом. 1, 4, 8, 9, 10; S = 141,8 м² × 2 сл. × 0,12 л/м² = 34,0 л, +10 % и 0,5 л на подкраску → ≥ 37,9 л; тара 8 × 5 л
2	Краска интерьерная водно-дисперсионная акриловая для акцентных стен, матовая, класс мокрого истирания 1 по EN 13300, база C; цвет Farrow & Ball No. 289 «Inchyra Blue — тёмный сине-серый», колеровка машинная	Farrow & Ball Modern Emulsion		Farrow & Ball	л	12,5		поз. К2 колерной карты; пом. 1, 8, 10; S = 37,0 м² × 2 сл. × 0,12 л/м² = 8,9 л, +10 % и 0,5 л на подкраску → ≥ 10,3 л; тара 2 × 5 л + 1 × 2,5 л
3	Краска интерьерная водно-дисперсионная акриловая для потолков, глубокоматовая, класс мокрого истирания 2 по EN 13300, база A; цвет NCS S 0502-Y «Белый с лёгкой желтизной», колеровка машинная	Tikkurila Anti-Reflex 2		Tikkurila	л	18,9		поз. К3 колерной карты; пом. 1, 2, 4, 7, 8, 9, 10; S = 67,8 м² × 2 сл. × 0,12 л/м² = 16,3 л, +10 % и 0,5 л на подкраску → ≥ 18,4 л; тара 2 × 9 л + 1 × 0,9 л
4	Краска интерьерная водно-дисперсионная акриловая для стен, матовая, класс мокрого истирания 1 по EN 13300, база A; цвет NCS S 0502-Y «Белый с лёгкой желтизной», колеровка машинная	Tikkurila Harmony		Tikkurila	л	9		поз. К5 колерной карты; пом. 2, 7; S = 29,5 м² × 2 сл. × 0,12 л/м² = 7,1 л, +10 % и 0,5 л на подкраску → ≥ 8,3 л; тара 1 × 9 л
5	Краска интерьерная водно-дисперсионная акриловая для стен, матовая, класс мокрого истирания 2 по EN 13300, база A; цвет Farrow & Ball No. 291 «School House White — тёплый меловой белый», колеровка машинная	Tikkurila Optiva 5 Matt		Tikkurila	л	7,5		поз. К7 колерной карты; пом. 3; S = 24,9 м² × 2 сл. × 0,12 л/м² = 6,0 л, +10 % и 0,5 л на подкраску → ≥ 7,1 л; тара 1 × 5 л + 1 × 2,5 л
6	Краска интерьерная водно-дисперсионная акриловая для акцентных стен, матовая, класс мокрого истирания 2 по EN 13300, база C; цвет Farrow & Ball No. 255 «Tanner's Brown — тёмный шоколад», колеровка машинная	Tikkurila Optiva 5 Matt		Tikkurila	л	7,5		поз. К8 колерной карты; пом. 3; S = 12,3 м² × 3 сл. × 0,12 л/м² = 4,4 л, +10 % и 0,5 л на подкраску → ≥ 5,4 л; тара 1 × 5 л + 1 × 2,5 л
7	Краска интерьерная водно-дисперсионная акриловая для потолков, глубокоматовая, класс мокрого истирания 2 по EN 13300, база A; цвет Farrow & Ball No. 291 «School House White — тёплый меловой белый», колеровка машинная	Tikkurila Anti-Reflex 2		Tikkurila	л	7,5		поз. К9 колерной карты; пом. 3; S = 20,3 м² × 2 сл. × 0,12 л/м² = 4,9 л, +10 % и 0,5 л на подкраску → ≥ 5,9 л; тара 1 × 5 л + 1 × 2,5 л
8	Краска интерьерная водно-дисперсионная акриловая для стен, полуматовая, класс мокрого истирания 1 по EN 13300, база A; цвет Farrow & Ball No. 291 «School House White — тёплый меловой белый», колеровка машинная	Tikkurila Luja 7		Tikkurila	л	7,5		поз. К12 колерной карты; пом. 5; S = 21,9 м² × 2 сл. × 0,12 л/м² = 5,2 л, +10 % и 0,5 л на подкраску → ≥ 6,3 л; тара 1 × 5 л + 1 × 2,5 л
9	Краска интерьерная водно-дисперсионная акриловая для потолков, матовая, класс мокрого истирания 1 по EN 13300, база A; цвет Farrow & Ball No. 291 «School House White — тёплый меловой белый», колеровка машинная	Tikkurila Luja 7		Tikkurila	л	2,5		поз. К13 колерной карты; пом. 5; S = 6,5 м² × 2 сл. × 0,12 л/м² = 1,6 л, +10 % и 0,5 л на подкраску → ≥ 2,2 л; тара 1 × 2,5 л
10	Краска интерьерная водно-дисперсионная акриловая для потолков, матовая, класс мокрого истирания 1 по EN 13300, база A; цвет NCS S 0502-Y «Белый с лёгкой желтизной», колеровка машинная	Tikkurila Luja 7		Tikkurila	л	2,7		поз. К14 колерной карты; пом. 6, 11; S = 6,0 м² × 2 сл. × 0,12 л/м² = 1,4 л, +10 % и 0,5 л на подкраску → ≥ 2,1 л; тара 1 × 2,7 л
11	Краска для МДФ и дерева в цвет Farrow & Ball No. 291 «School House White — тёплый меловой белый» — окраска плинтуса; блеск не ниже блеска стен	марка не задана			л	2,4		поз. К4, К10; пом. 1, 3, 4, 5, 8, 9, 10; L = 92,6 м, S = 8,9 м² × 2 сл. × 0,12 л/м² + 10 %; продукт подобрать в веере Farrow & Ball
12	Краска для МДФ и дерева в цвет NCS S 0502-Y «Белый с лёгкой желтизной» — окраска плинтуса; блеск не ниже блеска стен	марка не задана			л	0,5		поз. К6; пом. 2, 7; L = 10,8 м, S = 1,0 м² × 2 сл. × 0,12 л/м² + 10 %; продукт подобрать в веере NCS
13	Грунтовка акриловая под окраску стен и потолков — из системы производителя краски	по системе краски			м²	369		площадь окраски стен, акцентов и потолков; 1 слой перед окраской; расход — по ТУ грунтовки

					Проект: Квартира 103 м²	
	Лист	№ док.	Подпись	Дата	Спецификация отделочных материалов	Стадия / Лист / Листов
Дизайнер	Кырлан А.С.			18.10.26		П / С2 / 103


1 Порог 15 мм: мокрая зона — жилое помещение (М 1:10)

Применение: двери Д-5, Д-9

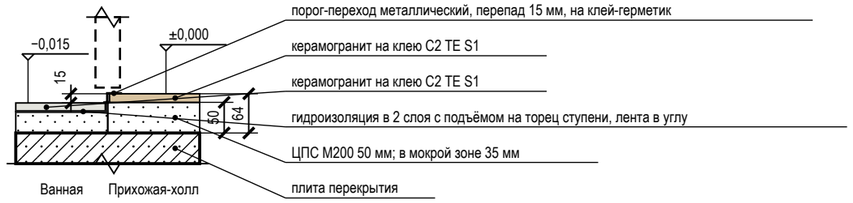


2 Дверь скрытого монтажа в плоскости стены, плинтус (М 1:5)

Применение: двери Д-2, Д-3, Д-4, Д-5, Д-6, Д-7, Д-8, Д-9

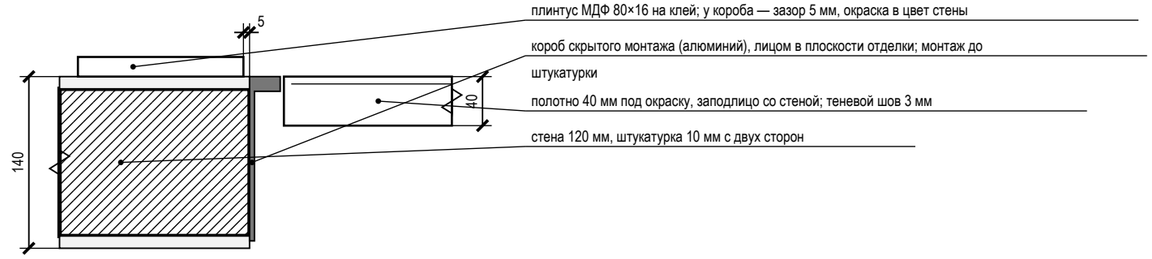


3 Короб стояков К1-1, К1-2 (кухня) с люком и звукоизоляцией (М 1:10)

Применение: пом. 6, 5, 11, 7

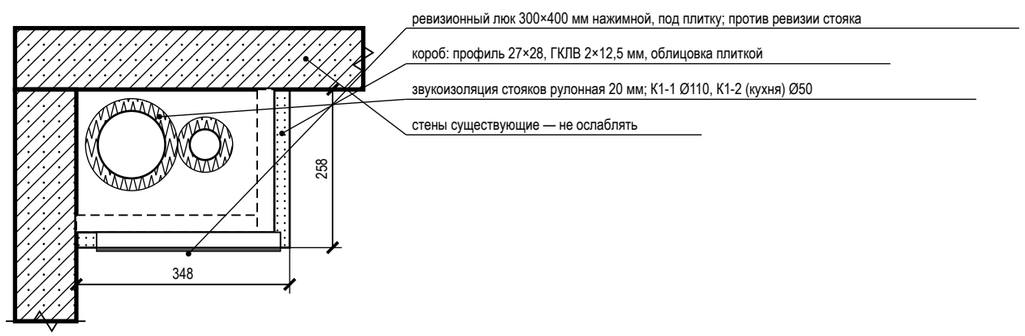


4 Гидроизоляция санузла: заход на стены 200 мм, примыкание ванны (М 1:20)

Применение: пом. 6, 11

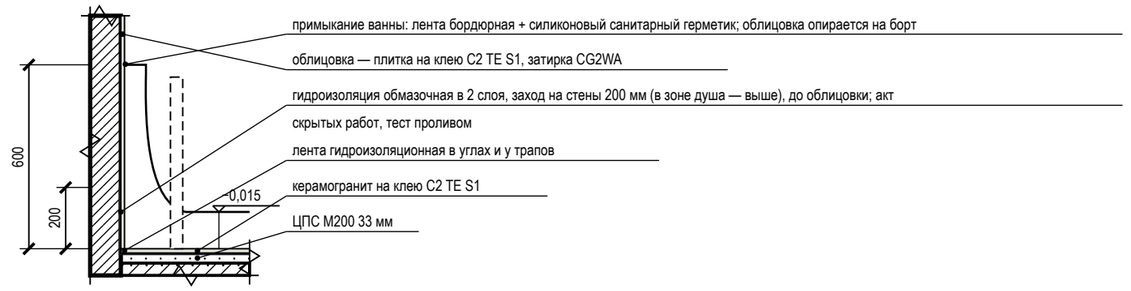

5 Плинтус МДФ 80×16 мм у окрашенной стены (М 1:10)

Применение: пом. 1, 2, 3, 4, 5, 7, 8, 9, 10

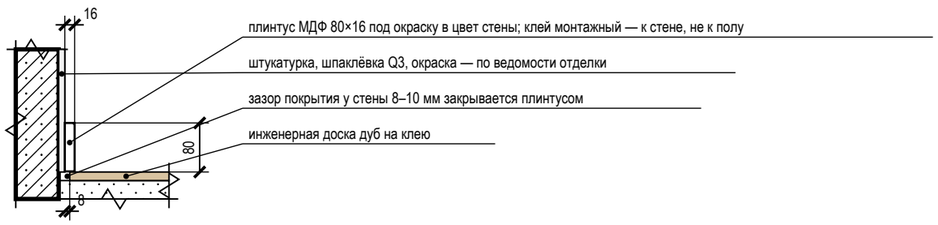

Условные обозначения

- железобетон (плита, стены)
- кладка, перегородка
- стяжка, раствор
- гипсокартон ГКЛВ
- звукоизоляция, эластичный заполнитель
- плитка, керамогранит на клею
- инженерная доска (покрытие пола)
- металлический профиль (порог, Т-профиль, короб двери)
- гидроизоляция (обмазочная, лента)

Примечания

1. Узлы — типовые решения проекта для мест, отмеченных выносками на листе схемы расположения развёрток и узлов; размеры — в мм, отметки — в м от ±0,000.
2. Узлы с гидроизоляцией, закладными и коробами скрытого монтажа принимаются по актам скрытых работ до закрытия отделкой; гидроизоляция — после теста проливом (24 ч).
3. Марки изделий (порог, Т-профиль, короб скрытой двери, люк) — по спецификациям; замена — на аналог с теми же габаритами по согласованию с автором проекта.

					Проект: Квартира 103 м²
	Лист	№ док.	Подпись	Дата	
Дизайнер	Кырлан А.С.			18.10.26	Узлы

Стадия	Лист	Листов
П	С3	103

выпуск 18.10.2026 № d119044df4 · стр. 103 из 103