LINEA

РАБОЧАЯ ДОКУМЕНТАЦИЯ

Дом 331 м²

Шифр комплекта ГД-2026-010-АИ

Стадия РП

Дата выпуска 18.10.2026

ПРЕДВАРИТЕЛЬНО · не для производства работ
открыто пунктов: 6 (реестр — л. 7)

ДИЗАЙНЕР

Кырлан Александр Сергеевич

выпуск 18.10.2026 · 9365d64cec · стр. 1 из 197

Содержание

ПРЕДВАРИТЕЛЬНО · не для производства работ · открыто пунктов: 6 (реестр — л. 7)

03 Общие данные 25 л.

28 Планировочное решение 11 л.

40 Электрооборудование 43 л.

84 Декор и текстиль 20 л.

105 Развёртки и узлы 50 л.

156 Смета 10 л.

167 Визуализации 30 л.

ДИЗАЙН-ПРОЕКТ ИНТЕРЬЕРА

Дом 331 м²

Шале

270,67 м²

защищённый · тёплый · основательный · природный · камерный · после мороза — у огня

Современное шале 60 % + эко (eco-organic.json) 40 %: загородный дом у леса. Стены — шерстяной белый Joa's White No. 226 и молочный S 0804-Y30R, потолки — известковый Slaked Lime No. 105; второй план — выцветший оливковый V451, шалфей S 3020-G30Y, песчаник X463; акценты — хвойный S 7020-G10Y, терракота Red Earth No. 64, брусника Eating Room Red No. 43. Дерево — дуб и лиственница под маслом, камень у камина.

ПАЛИТРА 60 / 30 / 10

F&B No. 226	NCS S 0804-Y30R	Little Greene No. 105	V451	NCS S 3020-G30Y
60 %	60 %	60 %	30 %	30 %

Визуализация 1 · Вид сверху (3D): планировка с мебелью, текстилем и декором

ОБЪЕКТ	ОБЩАЯ ПЛОЩАДЬ	ПОМЕЩЕНИЙ
Дом 331 м²	270,67 м²	20, из них жилых 6
СТИЛЬ	**СТАДИЯ**	**ШИФР**
Шале	Рабочий проект · предварительно	ГД-2026-010-АИ

АВТОР ПРОЕКТА

Кырлан Александр Сергеевич

Октябрь 2026

Изм.	Кол.уч	Лист	№ док.	Подп.	Дата
Разраб.		Кырлан А.С.			21.10.26
Пров.					
ГИП					
Н. контр.					
Утв.					

ГД-2026-010-АИ

Дом 331 м²

Общая площадь 270,67* м² · * размеры приняты, не замерены (реестр — л. 7, К-1)

Дизайн-проект интерьера	Стадия	Лист	Листов
	РП	1	159
Титульный лист М б/м	**Кырлан Александр Сергеевич**		

выпуск 18.10.2026 № 9365d64cec · стр. 3 из 197

Общие данные

Комплект ГД-2026-010-АИ · Дом 331 м² с мансардой и гаражом

ПРЕДВАРИТЕЛЬНО · не для производства работ · открыто пунктов: 6 (реестр — л. 7)

Допущения и предложения на листе. Знак «*» принято (замерить). См. лист открытых вопросов (лист 7).

Ведомость рабочих чертежей основного комплекта ГД-2026-010-АИ

Лист	Наименование	Примечание
1	Титульный лист	
2	Общие данные	
3	Общие данные	
4	Общие данные	
5	Общие данные	
6	Общие данные	
7	Открытые вопросы, принятые допущения и конфликты	
8	Задание на контрольный обмер и обследование. Лист 1 из 3	
9	Задание на контрольный обмер и обследование. Лист 2 из 3	
10	Задание на контрольный обмер и обследование. Лист 3 из 3	
11	График закупок и работ. Лист 1 из 4	
12	График закупок и работ. Лист 2 из 4	
13	График закупок и работ. Лист 3 из 4	
14	График закупок и работ. Лист 4 из 4	
15	Обмерный план · 1-й этаж	
16	Обмерный план · Мансарда	
17	План демонтажа и монтажа перегородок · 1-й этаж	
18	План демонтажа и монтажа перегородок · Мансарда	
19	План дверей и ведомость заполнения проёмов · 1-й этаж	
20	План дверей и ведомость заполнения проёмов · Мансарда	
21	Лестница Л-1*	
22	Концепция интерьера · 1-й этаж	
23	Концепция интерьера · Мансарда	
24	План расстановки мебели · 1-й этаж	
25	План расстановки мебели · Мансарда	
26	Спецификация мебели и оборудования	
27	Спецификация мебели и оборудования (продолжение)	
28	Спецификация мебели и оборудования (продолжение)	
29	Спецификация мебели и оборудования (продолжение)	
30	Спецификация мебели и оборудования (продолжение)	

Ведомость рабочих чертежей основного комплекта ГД-2026-010-АИ (продолжение)

Лист	Наименование	Примечание
31	План розеток и электровыводов · 1-й этаж	
32	План розеток и электровыводов · Мансарда	
33	План освещения · 1-й этаж	
34	План освещения · Мансарда	
35	План выключателей и схема включения · 1-й этаж	
36	План выключателей и схема включения · Мансарда	
37	Ведомость электроточек и изделий	
38	Ведомость электроточек и изделий (продолжение)	
39	Однолинейная схема щита	
40	Однолинейная схема щита (продолжение)	
41	План принципиальных трасс · 1-й этаж	
42	План принципиальных трасс · Мансарда	
43	План слаботочных сетей · 1-й этаж	
44	План слаботочных сетей · Мансарда	
45	План вентиляции · 1-й этаж	
46	План вентиляции · Мансарда	
47	План отопления · 1-й этаж	
48	План отопления · Мансарда	
49	План выводов сантехники · 1-й этаж	
50	План выводов сантехники · Мансарда	
51	Схема разводки водопровода и канализации · 1-й этаж	
52	Схема разводки водопровода и канализации · Мансарда	
53	Спецификация сантехнического оборудования	

Общие указания — лист 6: ±0,000 — чистый пол; несущие конструкции и сети дома — по отдельному проекту; скрытые работы — по актам. Открытые вопросы и допущения — лист 7.

Изм.	Кол.уч	Лист	№ док.	Подп.	Дата
Разраб.		Кырлан А.С.			21.10.26
Пров.					
ГИП					
Н. контр.					
Утв.					

ГД-2026-010-АИ

Дом 331 м²

Общая площадь 270,67* м² · * размеры приняты, не замерены (реестр — л. 7, К-1)

Дизайн-проект интерьера

Стадия	Лист	Листов
РП	2	159

Общие данные

М б/м

Кырлан Александр Сергеевич

выпуск 18.10.2026 № 9365d64cec · стр. 4 из 197

Общие данные

Комплект ГД-2026-010-АИ · лист 2 общих данных (продолжение)

ПРЕДВАРИТЕЛЬНО · не для производства работ · открыто пунктов: 6 (реестр — л. 7)

Ведомость рабочих чертежей основного комплекта ГД-2026-010-АИ (продолжение)

Лист	Наименование	Примечание
54	Спецификация светильников и сценарии освещения	
55	План потолков · 1-й этаж	
56	План потолков · Мансарда	
57	Разрезы и узлы потолков	
58	Разрезы и узлы потолков (продолжение)	
59	Разрезы и узлы потолков (продолжение)	
60	Разрезы и узлы потолков (продолжение)	
61	Раскладка плитки. Планы полов	
62	Раскладка плитки. Котельная. Прихожая. Тамбур. Веранда	
63	Раскладка плитки. Крыльцо	
64	Раскладка плитки. Санузел 1 этажа. Развёртки стен	
65	Раскладка плитки. Санузел мастер. Развёртки стен	
66	Раскладка плитки. Санузел 2. Развёртки стен	
67	План полов · 1-й этаж	
68	План полов · Мансарда	
69	Конструкции полов и стыки покрытий	
70	Ведомость отделки помещений. Лист 1 из 3	
71	Ведомость отделки помещений. Лист 2 из 3	
72	Ведомость отделки помещений. Лист 3 из 3	
73	Колерная карта	
74	Колерная карта	
75	Спецификация отделочных материалов	
76	Спецификация отделочных материалов	
77	Концепция декора и визуализации	
78	План текстиля и декора · 1-й этаж	
79	План текстиля и декора · Мансарда	
80	Шторы и карнизы	
81	Ведомость текстиля	Допущения и предложения на листе. См. лист открытых вопросов (лист 7).
82	Ведомость текстиля (продолжение)	
83	Ведомость декора. Схемы развески	

Ведомость рабочих чертежей основного комплекта ГД-2026-010-АИ (продолжение)

Лист	Наименование	Примечание
84	Встроенная мебель. Схема расположения · 1-й этаж	
85	Встроенная мебель. Схема расположения · Мансарда	
86	Система хранения Кт1	
87	Система хранения Кл1	
88	Шкаф-купе Пр1	
89	Система хранения Гр1	
90	Система хранения Гм2	
91	Шкаф распашной С3	
92	Система хранения Сп3	
93	Шкаф распашной Д3	
94	Шкаф распашной Д6	
95	Кухня (пом. 1). Развёртка гарнитура	
96	Кухня (пом. 1). Монтажная схема	
97	Шкафы. Монтажная схема. Лист 1 из 2	
98	Шкафы. Монтажная схема. Лист 2 из 2	
99	Ведомости изделий, техники и фурнитуры	
100	Реестр марок отделки и позиций альбома	
101	Реестр марок отделки и позиций альбома (продолжение)	
102	Схема расположения развёрток и узлов	
103	Развёртка стены А. Кухня-столовая (пом. 1), кухонный фронт	
104	Развёртки стен Б, В. Кухня-столовая (пом. 1)	
105	Развёртка стены Г. Кухня-столовая (пом. 1)	
106	Развёртки стен А, Б. Кабинет-гостевая (пом. 2)	

Общие указания — лист 6: ±0,000 — чистый пол; несущие конструкции и сети дома — по отдельному проекту; скрытые работы — по актам. Открытые вопросы и допущения — лист 7.

Изм.	Кол.уч	Лист	№ док.	Подп.	Дата
Разраб.		Кырлан А.С.			21.10.26
Пров.					
ГИП					
Н. контр.					
Утв.					

ГД-2026-010-АИ

Дом 331 м²

Общая площадь 270,67* м² · * размеры приняты, не замерены (реестр — л. 7, К-1)

Дизайн-проект интерьера

Стадия	Лист	Листов
РП	3	159

Общие данные

М б/м

Кырлан Александр Сергеевич

выпуск 18.10.2026 № 9365d64cec · стр. 5 из 197

Общие данные

Комплект ГД-2026-010-АИ · лист 3 общих данных (продолжение)

Допущения и предложения на листе. См. лист открытых вопросов (лист 7).

Ведомость рабочих чертежей основного комплекта ГД-2026-010-АИ (продолжение)

Лист	Наименование	Примечание
107	Развёртки стен В, Г. Кабинет-гостевая (пом. 2)	
108	Развёртка стены А. Санузел 1 этажа (пом. 3)	
109	Развёртки стен Б, В. Санузел 1 этажа (пом. 3)	
110	Развёртка стены Г. Санузел 1 этажа (пом. 3)	
111	Развёртки стен. Котельная (пом. 4)	
112	Развёртка стены А. Гостиная (пом. 5)	
113	Развёртка стены Б. Гостиная (пом. 5)	
114	Развёртка стены В. Гостиная (пом. 5)	
115	Развёртка стены Г. Гостиная (пом. 5)	
116	Развёртки стен. Холл с лестницей (пом. 6)	
117	Развёртки стен. Кладовая (пом. 7)	
118	Развёртки стен А, Б. Прихожая (пом. 8)	
119	Развёртки стен В, Г. Прихожая (пом. 8)	
120	Развёртки стен. Тамбур (пом. 9)	
121	Развёртка стены А. Гараж (пом. 10)	
122	Развёртка стены Б. Гараж (пом. 10)	
123	Развёртка стены В. Гараж (пом. 10)	
124	Развёртка стены Г. Гараж (пом. 10)	
125	Развёртка стены А. Веранда (пом. 11)	
126	Развёртка стены В. Веранда (пом. 11)	
127	Развёртка стены Г. Веранда (пом. 11)	
128	Развёртки стен. Крыльцо (пом. 12)	
129	Развёртки стен А, Б. Спальня мастер (пом. 13)	
130	Развёртки стен В, Г. Спальня мастер (пом. 13)	
131	Развёртки стен А, Б, В. Гардеробная мастер (пом. 14)	
132	Развёртка стены Г. Гардеробная мастер (пом. 14)	
133	Развёртка стены А. Санузел мастер (пом. 15)	
134	Развёртка стены Б. Санузел мастер (пом. 15)	
135	Развёртка стены В. Санузел мастер (пом. 15)	
136	Развёртка стены Г. Санузел мастер (пом. 15)	

Ведомость рабочих чертежей основного комплекта ГД-2026-010-АИ (продолжение)

Лист	Наименование	Примечание
137	Развёртки стен А, Б. Спальня 2 (пом. 16)	
138	Развёртки стен В, Г. Спальня 2 (пом. 16)	
139	Развёртки стен А, Б. Холл мансарды (пом. 17)	
140	Развёртка стены В. Холл мансарды (пом. 17)	
141	Развёртка стены Г. Холл мансарды (пом. 17)	
142	Развёртки стен А, Б. Спальня 3 (пом. 18)	
143	Развёртки стен В, Г. Спальня 3 (пом. 18)	
144	Развёртки стен А, Б. Спальня 4 (пом. 19)	
145	Развёртки стен В, Г. Спальня 4 (пом. 19)	
146	Развёртка стены А. Санузел 2 (пом. 20)	
147	Развёртки стен Б, В. Санузел 2 (пом. 20)	
148	Развёртка стены Г. Санузел 2 (пом. 20)	
149	Узлы	
150	Ведомость объёмов работ	
151	Ведомость объёмов работ (продолжение)	
152	Ведомость объёмов работ (продолжение)	
153	Ведомость объёмов работ (продолжение)	
154	Ведомость объёмов работ (окончание)	
155	Спецификация материалов	
156	Спецификация материалов (продолжение)	
157	Спецификация материалов (окончание)	
158	Смета ориентировочная	
159	Смета ориентировочная (окончание)	

Общие указания — лист 6: ±0,000 — чистый пол; несущие конструкции и сети дома — по отдельному проекту; скрытые работы — по актам. Открытые вопросы и допущения — лист 7.

Изм.	Кол.уч	Лист	№ док.	Подп.	Дата	ГД-2026-010-АИ		
						Дом 331 м²		
						Общая площадь 270,67* м² · * размеры приняты, не замерены (реестр — л. 7, К-1)		
Разраб.		Кырлан А.С.			21.10.26	Дизайн-проект интерьера	Стадия	Лист	Листов
Пров.							РП	4	159
ГИП									
						Общие данные	Кырлан Александр Сергеевич		
Н. контр.						М б/м			
Утв.									

выпуск 18.10.2026 № 9365d64cec · стр. 6 из 197

Общие данные

Комплект ГД-2026-010-АИ · лист 4 общих данных (продолжение)

Ведомость ссылочных и прилагаемых документов

Обозначение	Наименование	Примечание
	Ссылочные документы	
ГОСТ 21.201-2011	СПДС. Условные графические изображения элементов зданий, сооружений и конструкций	
ГОСТ 21.205-2016	СПДС. Условные обозначения элементов санитарно-технических систем	
ГОСТ 21.210-2014	СПДС. Изображения условные графические электрооборудования и проводок на планах	
ГОСТ 2.306-68	ЕСКД. Обозначения графические материалов и правила их нанесения на чертежах	
	Прилагаемые документы	
ГД-2026-010-АИ.В1	Визуализация. Вид сверху (3D): планировка с мебелью, текстилем и декором	альбом визуализаций
ГД-2026-010-АИ.В2	Визуализация. Вид сверху (3D): планировка с мебелью, текстилем и декором	
ГД-2026-010-АИ.В3	Визуализация. Визуализация «room-balcony1-wC»	
ГД-2026-010-АИ.В4	Визуализация. Визуализация «room-balcony2-wide»	
ГД-2026-010-АИ.В5	Визуализация. Визуализация «room-bath1-wide»	
ГД-2026-010-АИ.В6	Визуализация. Визуализация «room-bath2-wide»	
ГД-2026-010-АИ.В7	Визуализация. Визуализация «room-bath3-wide»	
ГД-2026-010-АИ.В8	Визуализация. Визуализация «room-bedroom1-wA»	
ГД-2026-010-АИ.В9	Визуализация. Визуализация «room-bedroom1-wC»	
ГД-2026-010-АИ.В10	Визуализация. Визуализация «room-bedroom2-wA»	
ГД-2026-010-АИ.В11	Визуализация. Визуализация «room-bedroom2-wB»	
ГД-2026-010-АИ.В12	Визуализация. Визуализация «room-corridor1-wide»	
ГД-2026-010-АИ.В13	Визуализация. Визуализация «room-corridor2-wide»	
ГД-2026-010-АИ.В14	Визуализация. Визуализация «room-hall1-wA»	
ГД-2026-010-АИ.В15	Визуализация. Визуализация «room-hall1-wB»	
ГД-2026-010-АИ.В16	Визуализация. Визуализация «room-kids1-wA»	
ГД-2026-010-АИ.В17	Визуализация. Визуализация «room-kids1-wC»	
ГД-2026-010-АИ.В18	Визуализация. Визуализация «room-kids2-wA»	
ГД-2026-010-АИ.В19	Визуализация. Визуализация «room-kids2-wC»	
ГД-2026-010-АИ.В20	Визуализация. Визуализация «room-kitchen-wA»	
ГД-2026-010-АИ.В21	Визуализация. Визуализация «room-kitchen-wD»	
ГД-2026-010-АИ.В22	Визуализация. Визуализация «room-living-wA»	

Ведомость ссылочных и прилагаемых документов (продолжение)

Обозначение	Наименование	Примечание
ГД-2026-010-АИ.В23	Визуализация. Визуализация «room-living-wC»	
ГД-2026-010-АИ.В24	Визуализация. Визуализация «room-living-wD»	
ГД-2026-010-АИ.В25	Визуализация. Визуализация «room-storage1-wide»	
ГД-2026-010-АИ.В26	Визуализация. Визуализация «room-storage2-wide»	
ГД-2026-010-АИ.В27	Визуализация. Визуализация «room-storage3-wide»	
ГД-2026-010-АИ.В28	Визуализация. Визуализация «room-study-wA»	
ГД-2026-010-АИ.В29	Визуализация. Визуализация «room-study-wD»	
ГД-2026-010-АИ.В30	Визуализация. Визуализация «room-wardrobe-wide»	

Допущения и предложения на листе

Основа листа: размеры и контуры этажей подобраны проектировщиком по составу помещений и площадям этажей с картинки 470 px (размеры на ней не читаются); обмер и исходный проект — задание (К-1); высоты: 1-й этаж 2800 мм, мансарда 2700 мм (горизонтальная часть) приняты; скаты кровли мансарды приняты по картинке: колено 1200 мм, уклон 45°, конёк вдоль длинной стороны; проект КР — задание (К-2); наружные стены 400 мм, перегородки 120 мм приняты (К-1); разрешённая мощность 15 кВт принята по типовым ТУ для частного дома (К-4); подрайон климата не задан — принят не северный (жилые от 2,5 м) (К-7).

См. лист открытых вопросов (лист 7, записи К-1, К-2, К-4, К-7).

Общие указания — лист 6: ±0,000 — чистый пол; несущие конструкции и сети дома — по отдельному проекту; скрытые работы — по актам. Открытые вопросы и допущения — лист 7.

Изм.	Кол.уч	Лист	№ док.	Подп.	Дата
Разраб.		Кырлан А.С.			21.10.26
Пров.					
ГИП					
Н. контр.					
Утв.					

ГД-2026-010-АИ

Дом 331 м²

Общая площадь 270,67* м² · * размеры приняты, не замерены (реестр — л. 7, К-1)

Дизайн-проект интерьера

Стадия	Лист	Листов
РП	5	159

Общие данные

М б/м

Кырлан Александр Сергеевич

выпуск 18.10.2026 № 9365d64cec · стр. 7 из 197

Общие данные

Комплект ГД-2026-010-АИ · лист 5 общих данных (продолжение)

Состав дизайн-проекта

Раздел	Состав	Листы
Обложка	Дизайн-проект интерьера; Дом 331 м²; автор проекта — Кырлан Александр Сергеевич	1 с.
Концепция	Стиль Шале 60 % + Эко и органический модерн 40 %: концепция интерьера, палитра и материалы (колерная карта — лист 73)	л. 22
Визуализации	30 изобр.: Вид сверху (3D): планировка с мебелью, текстилем и декором; Вид сверху (3D): планировка с мебелью, текстилем и декором; Визуализация «room-balcony1-wC»; Визуализация «room-balcony2-wide»; Визуализация «room-bath1-wide»; Визуализация «room-bath2-wide»; Визуализация «room-bath3-wide»; Визуализация «room-bedroom1-wA»; Визуализация «room-bedroom1-wC»; Визуализация «room-bedroom2-wA»; Визуализация «room-bedroom2-wB»; Визуализация «room-corridor1-wide»; Визуализация «room-corridor2-wide»; Визуализация «room-hall1-wA»; Визуализация «room-hall1-wB»; Визуализация «room-kids1-wA»; Визуализация «room-kids1-wC»; Визуализация «room-kids2-wA»; Визуализация «room-kids2-wC»; Визуализация «room-kitchen-wA»; Визуализация «room-kitchen-wD»; Визуализация «room-living-wA»; Визуализация «room-living-wC»; Визуализация «room-living-wD»; Визуализация «room-storage1-wide»; Визуализация «room-storage2-wide»; Визуализация «room-storage3-wide»; Визуализация «room-study-wA»; Визуализация «room-study-wD»; Визуализация «room-wardrobe-wide»	В1–В30
Рабочие чертежи	планы, развёртки, узлы (развёртки и узлы — листы 102, 104, 106, 107, 109, 111, 116–120, 128–131, 137–139, 142–145, 147, 149)	л. 1–159
Спецификации и ведомости	оборудование, изделия, отделка, электроточки	л. 19, 20, 26–30, 37, 38, 53, 54, 70–76, 81–83, 150–157

Условные обозначения

- контрольный отрезок 1000 мм натуры: по нему проверяют печать 1:1
- отметка уровня, м: ±0,000 — чистый пол жилых помещений
- А — марка развёртки: буква стены, стрелка — взгляд
- О1 — марка отделки по реестру отделки альбома
- выноска узла: над полкой — узел, под полкой — лист

Общие указания

1. Рабочие чертежи интерьера разработаны на основании задания на проектирование и обмерного плана (лист 15). Объект: Дом 331 м²; автор проекта — Кырлан Александр Сергеевич; общая площадь 270,67 м², жилая 119,16 м², помещений 18.
2. Рабочие чертежи выполнены в соответствии с заданием на проектирование и нормативными документами, перечисленными в п. 4.
3. Открытые вопросы, принятые допущения и конфликты между разделами, не снятые к выпуску комплекта, сведены в таблицы на листе 7. До ответа по пункту таблицы показанное на указанном там листе — допущение, а не утверждённое решение: комплект по этим листам предварительный.
4. Нормативные документы, на которые есть ссылки в листах комплекта: ГОСТ Р 21.101-2026; ГОСТ 21.501-2018; ГОСТ 2.302-68; ГОСТ 2.303-68; ГОСТ 2.304-81; ГОСТ 2.307-2011; СП 54.13330.2022; СП 71.13330.2017; СП 73.13330.2016; ПУЭ (7-е изд.), гл. 1.8, 7.1; ГОСТ Р 50571.7.701-2024; СанПиН 1.2.3685-21; ГОСТ 2.702; ГОСТ 2.755; ГОСТ 21.110-2013; ГОСТ 13996-2019; ГОСТ 25772-2025; ГОСТ 31565-2012; ГОСТ 31975; ГОСТ 32414-2013; ГОСТ 32415-2013; ГОСТ Р 56387-2018; СП 20.13330.2016; СП 29.13330.2011; СП 51.13330.2011; СП 55.13330.2016; СП 59.13330.2020; СП 131.13330. Документы из ведомости ссылочных документов здесь не повторяются.
5. За отметку ±0,000 принят уровень чистого пола жилых помещений квартиры (относительная отметка; абсолютная — по проекту дома). Отметка чистого пола мокрых помещений — −0,015. Размеры — в миллиметрах, отметки — в метрах, площади — в м²; высоты установки Н от чистого пола своего помещения до оси изделия.
6. Несущие конструкции, общедомовые стояки, вентиляционные каналы и инженерные сети дома настоящим комплектом не изменяются. Работы, затрагивающие их (проём или штраба в несущей стене, перенос стояка, врезка в вентканал, расширение мокрой зоны), выполняются только по отдельному проекту, к которому прилагается техническое заключение о допустимости и безопасности работ, выданное автором проекта дома или организацией с допуском на обследование, и который согласован в установленном порядке (Жилищный кодекс РФ, ст. 25–29).
7. Трассы инженерных сетей на листах — принципиальные. Расчёты электрических нагрузок и токов КЗ, гидравлики, воздухообмена, освещённости и нагрузок на перекрытие выполняются в проектах ЭОМ, ВК, ОВ и КР организацией с допуском СРО; фактические трассы до закрытия отделкой фиксируются исполнительными схемами.
8. Стиль интерьера — Шале 60 % + Эко и органический модерн 40 %. Палитра проекта: основной 60 % — Farrow & Ball No. 226 «Joa's White», NCS S 0804-Y30R «S 0804-Y30R», Little Greene No. 105 «Slaked Lime»; дополнительный 30 % — Tikkurila V451 «Olive grove V451», NCS S 3020-G30Y «S 3020-G30Y», Tikkurila X463 «Sandstone X463», Farrow & Ball No. 229 «Elephant's Breath — тёплый средне-серый с лиловым подтоном», Farrow & Ball No. 40 «Mouse's Back — тёплый коричнево-серый», Farrow & Ball No. 243 «Charleston Gray — серо-коричневый «камень»», NCS S 2005-Y20R «Светлый песочно-серый», NCS S 3010-Y30R «S 3010-Y30R»; акцент 10 % — NCS S 7020-G10Y «Хвойный тёмно-зелёный», Farrow & Ball No. 64 «Red Earth», Farrow & Ball No. 43 «Eating Room Red — брусничный красный». Коды цвета — по веерам производителей; цвет утверждается по выкрасу на объекте при освещении проекта.
9. Площади поверхностей — по чистым граням стен до отделки: стены = периметр × высоту от чистого пола помещения до низа потолка минус проёмы (облицовка плиткой — до верха облицовки); плинтус = периметр минус дверные проёмы; пол и потолок — по площади помещения. Количество плиток — по раскладке. Способ один для всех листов комплекта (ведомость отделки, колерная карта, раскладка плитки, развёртки).
10. Марки: стены помещения на всех листах — А (верхняя по плану), Б (правая), В (нижняя), Г (левая); марка отделки О — одна на весь альбом; реестр марок отделки (с позициями колерной карты той же отделки) и марки позиций по видам — на листе 100.
11. Развёртки стен выполнены по всем помещениям для стен с электроточками, мебелью, декором и отделкой: санузлы и кухонный фронт — в М 1:25, остальные стены — в М 1:40; расположение развёрток и узлов — на листе 102, узлы — на листе 149.
12. Перечень скрытых работ, на которые составляются акты освидетельствования (форма по приказу Минстроя России № 344/пр): гидроизоляция пола и стен мокрых помещений (с тестом проливом); стяжка пола (толщина, прочность, влажность основания); звукоизоляционные слои и демпферная лента; скрытая электропроводка (за потолком и в штробах стен; условия штробления — в следующем пункте); трубопроводы водоснабжения и канализации до закрытия (опрессовка, уклоны); закладные и усиления под подвесные приборы, мебель и тяжёлый декор, рамы инсталляций; короба дверей скрытого монтажа до штукатурки; каркасы ГКЛ потолков, коробов и перегородок до обшивки.
13. Скрытая электропроводка: за потолком и в штробах стен. Штробы в стенах выполняются только после технического заключения о несущих конструкциях; до заключения несущие стены не определены, и все стены считаются несущими; объём штроб — в ведомости объёмов работ, строка «Штробы в стенах» (вертикальные спуски; объём не меньше фактического, горизонтальные трассы — по исполнительной схеме).
14. Критерии приёмки: допуски отделочных покрытий — по СП 71.13330.2017; испытания систем водоснабжения и канализации — по СП 73.13330.2016 до закрытия трасс; приёмо-сдаточные испытания электроустановки — по ПУЭ, гл. 1.8, с протоколом электролаборатории.
15. Осознанные отступления от ГОСТ Р 21.101-2026, принятые в комплекте: номер листа и число листов («Листов») указаны на каждом листе; на масштабных листах в основной надписи указан фактический масштаб и дан контрольный отрезок 1000 мм; развёртки стен выполнены в М 1:25 и 1:40 (ГОСТ 21.507-81 — 1:50…1:500) ради читаемости привязок; размерные числа и марки элементов (Д-1, ОК-1, О6) — кеглем 2,5 мм, номера помещений — в кружке Ø 8 мм (канон — 3,5 мм и Ø 12 мм): так насыщенные листы А3 читаются без наложений надписей.
16. Графы «Пров.», «Н. контр.», «Утв.» основной надписи заполняются при согласовании комплекта с заказчиком; до согласования комплект подписывает автор проекта (графа «Разраб.»).

Допущения и предложения на листе

Основа листа: размеры и контуры этажей подобраны проектировщиком по составу помещений и площадям этажей с картинки 470 px (размеры на ней не читаются); обмер и исходный проект — задание (К-1); высоты: 1-й этаж 2800 мм, мансарда 2700 мм (горизонтальная часть) приняты; скаты кровли мансарды приняты по картинке: колено 1200 мм, уклон 45°, конёк вдоль длинной стороны; проект КР — задание (К-2); наружные стены 400 мм, перегородки 120 мм приняты (К-1); разрешённая мощность 15 кВт принята по типовым ТУ для частного дома (К-4); подрайон климата не задан — принят не северный (жилые от 2,5 м) (К-7).

См. лист открытых вопросов (лист 7, записи К-1, К-2, К-4, К-7).

Изм.	Кол.уч	Лист	№ док.	Подп.	Дата	ГД-2026-010-АИ		
						Дом 331 м²		
						Общая площадь 270,67* м² · * размеры приняты, не замерены (реестр — л. 7, К-1)		
Разраб.		Кырлан А.С.			21.10.26	Дизайн-проект интерьера	Стадия: РП	Лист: 6 / Листов: 159
Пров.								
ГИП								
Н. контр.						Общие данные	Кырлан Александр Сергеевич	
Утв.						М б/м		

выпуск 18.10.2026 № 9365d64cec · стр. 8 из 197

Открытые вопросы, принятые допущения и конфликты

ПРЕДВАРИТЕЛЬНО · не для производства работ · открыто пунктов: 6 (реестр — л. 7)

Сводка по реестрам координации (стартовое совещание 18.10.2026)

Комплект предварительный по пунктам этих таблиц. Пока по пункту нет ответа или решения, показанное на указанном листе — допущение проектировщика, а не утверждённое решение.
Сводка: открытых вопросов — 6 (из них ждут факта объекта — 4: контрольного обмера, обследования или документа).
Пункты, ответ на которые лежит на объекте, а не за столом проектировщика (графа «Вид», строка «Ждёт»), собраны на листе «Задание на контрольный обмер и обследование» (листы 8–10): что и где замерить, с какой точностью и чем подтвердить. Пункты, ждущие решения человека, на объекте не закрываются.

Открытые вопросы и принятые допущения

№	Формулировка	Вид	Кто решает	Если решения нет	Лист, где это проявляется
К-1	Размеры дома на картинке заказчика (470 px) не читаются: состав помещений и форма сняты с картинки, размеры подобраны проектировщиком под площади этажей 185,80 и 145,73 м². Нужен исходный проект дома (АР) или обмер.	Отсутствует Ждёт: обмера	Архитектор-планировщик	размеры на листах — предложение проектировщика; мебель на заказ и материалы по ним не заказывать	л. 15, 16 — Обмерный план л. 15, 17, 19, 22, 24, 31, 33, 35, 41, 43, 45, 47, 49, 51, 55, 64, 67, 78, 84, 108–110 — 1-й этаж л. 24, 25 — План расстановки мебели л. 15, 17, 19, 22, 24, 31, 33, 35, 41, 43, 45, 47, 49, 51, 55, 64, 67, 78, 84, 108–110 — 1-й этаж
К-2	Высоты этажей и кровля не известны: приняты 2800 мм (1-й этаж) и 2700 мм (горизонтальная часть потолка мансарды); скаты двускатная кровля, конёк вдоль длинной стороны, колено 1200 мм, уклон 45° (по перспективе и фасаду с картинки).	Отсутствует	Архитектор-планировщик	высоты — принятые, уточнить по проекту АР	л. 15, 16 — Обмерный план л. 15, 17, 19, 22, 24, 31, 33, 35, 41, 43, 45, 47, 49, 51, 55, 64, 67, 78, 84, 108–110 — 1-й этаж л. 55, 56 — План потолков л. 15, 17, 19, 22, 24, 31, 33, 35, 41, 43, 45, 47, 49, 51, 55, 64, 67, 78, 84, 108–110 — 1-й этаж
К-4	Разрешённая мощность дома по ТУ неизвестна, принята 15 кВт.	Отсутствует	Инженер-электрик	щит и группы рассчитаны на 15 кВт; при меньших ТУ пересчёт	л. 39 — Однолинейная схема щита л. 31, 32 — План розеток и электровыводов л. 15, 17, 19, 22, 24, 31, 33, 35, 41, 43, 45, 47, 49, 51, 55, 64, 67, 78, 84, 108–110 — 1-й этаж
К-5	Планировка этажей — предложение проектировщика по составу помещений с картинки (несущие стены, лестница, перекрытие не известны): нужен проект АР/КР дома.	Отсутствует Ждёт: документа	Архитектор-планировщик	перегородки и проёмы — предложение, к строительству не выдаются	л. 15, 16 — Обмерный план л. 15, 17, 19, 22, 24, 31, 33, 35, 41, 43, 45, 47, 49, 51, 55, 64, 67, 78, 84, 108–110 — 1-й этаж
К-6	Лестница Л-1 на картинке заказчика — одномаршевая в холле 1-го этажа (3,0×3,6 м), видно 11 проступей. До пола мансарды +3,150 нужно 18 подъёмов по 175 мм (равные ступени — СП 55.13330.2016 п. 8.2), то есть 17 проступей по 280 мм = 4,76 м длины марша; в холл 3,48 м в свету одномаршевая не встаёт (не хватает 1,66 м). Варианты: Г-образная с 3 забежными ступенями (8 + 3 + 6 подъёмов по 175 — встаёт в холл 3,24×2,68 м; при детях забежные — компромисс), Г-образная с площадкой (9 + 7 подъёмов по 197 мм — круче практики 150–180, для дома допустимо: уклон не нормируется, СП 55 п. 7.5), перенос лестницы или иная высота этажа по проекту АР/КР. Нужны: решение по типу марша и проект АР/КР (высота этажа, перекрытие, проём).	Отсутствует Ждёт: обмера, затем решения	Архитектор-планировщик	марш на планах и лист «Лестница Л-1» — по картинке (11 проступей, до отм. +2,100), ограждение и проём считаются по этому габариту; изделие не заказывать, проём в перекрытии не резать	architect/stairs-л-1 (лист по названию не найден)
К-7	Климатический подрайон (СП 131.13330) не задан: принят не северный — жилые комнаты и кухня под потолком от 2,5 м (СП 54, п. 5.12); в IA, IБ, IГ, IД, IVA — от 2,7 м.	Отсутствует Ждёт: документа	Архитектор-планировщик	отметки потолков жилых — по 2,5 м; при северном подрайоне уровни ниже 2,7 м пересчитать до заказа каркаса	л. 55, 56 — План потолков л. 15, 17, 19, 22, 24, 31, 33, 35, 41, 43, 45, 47, 49, 51, 55, 64, 67, 78, 84, 108–110 — 1-й этаж

Примечания

1. Номера листов — по ведомости рабочих чертежей комплекта (лист «Общие данные»).
2. Графа «Если решения нет» показывает состояние решения на листах; влияние на сроки и стоимость по пунктам не оценивалось.
3. Пункт, по которому принято решение, при следующем выпуске комплекта из таблиц исключается.

Изм.	Кол.уч	Лист	№ док.	Подп.	Дата	ГД-2026-010-АИ			
						Дом 331 м² Общая площадь 270,67* м² · * размеры приняты, не замерены (реестр — л. 7, К-1)			
Разраб.		Кырлан А.С.			21.10.26	Дизайн-проект интерьера	Стадия	Лист	Листов
Пров.							РП	7	159
ГИП									
						Открытые вопросы, принятые допущения и конфликты М б/м	**Кырлан Александр Сергеевич**		
Н. контр.									
Утв.									

Задание на контрольный обмер и обследование. Лист 1 из 3

ПРЕДВАРИТЕЛЬНО · не для производства работ · открыто пунктов: 6 (реестр — л. 7)

Что замерить, вскрыть и получить до заказа материалов и изделий

Задание собрано из открытых вопросов, ответ на которые лежит на объекте или в документах, а не за столом проектировщика. Пока факт не получен, размер, материал или положение на листах — допущение (знак «*»), а не замер.
Сводка: на объекте — 9 (до демонтажа — 7; после демонтажа — 2); документом и при закупке — 3; из допущений в данных и на листах — 9, из них без вопроса в реестре — 5. Закрываются вопросы: К-1, К-2, К-4–К-7 (6). Вопросы, ждущие решения человека, задание не закрывает — они решаются по реестру открытых вопросов.

Условия проведения

Порядок работ	Приёмы и точность	Кто присутствует	Если факт не совпал с проектом
1. До демонтажа — существующее состояние: контур, диагонали, высоты, проёмы, оси стояков, ниши и конструкции, которые видны. 2. После демонтажа, до черновых работ — то, что закрывали отделка и короба: основание стен, фактические толщины, углы, узлы. 3. Документы и данные закупки — не на объекте: к сроку из последней таблицы, от них зависят привязки и заказ. Что заказывается по размеру из задания, до закрытия пункта не заказывают: сроки изготовления — по графику закупок прораба.	Обход по часовой стрелке от входа: стены, проёмы, потолок, коммуникации (стояки, щиток, вентканалы), особенности (ниши, короба, выступы). Размеры записывают в мм; сумма участков равна общему размеру, при цепочке длиннее трёх участков ставят проверочный (общий) размер. Диагонали каждого помещения; если две диагонали различаются на 5 мм и больше, разницу подписывают на плане. Потолок — в нескольких точках: центр, углы, у проёмов. Проём — ширина, высота, глубина откоса, привязка к ближайшим углам, высота подоконника. Допустимая погрешность прибора — 2–3 мм на метр; размеры округляют кратно 5 мм; два контрольных промера одного размера не должны расходиться более чем на 2 %. Допуск по пункту — в графе «Точность». План БТИ обмер не заменяет.	Прораб (отвечает за проведение) — назначает день и порядок обхода, открывает объект и освобождает помещения, ведёт это задание и реестр изменений. Архитектор — выполняет обмер, составляет акт контрольного обмера и подписывает результаты по размерам и конструкциям. Владельцы вопросов присутствуют при пунктах своего раздела или принимают результат до заказа: Инженер ВК (вода, канализация) позиции О-1; Инженер-электрик — К-4; позиции О-2; Инженер ОВ позиции О-3; Отделочник — позиции О-8, О-9. Заказчик или его представитель — передаёт документы (план БТИ, проект дома, технические условия, паспорта), подписывает акт. Проектных решений на обмере не принимают: обмер даёт факт, решения — по реестру открытых вопросов (лист 7).	1. В пределах допуска пункта — принимается измеренное значение, лист перевыпускается, знак «*» снимается. 2. Больше допуска или контрольные промеры расходятся более чем на 2 % — промер повторяют; не подтвердилось — запись в реестр изменений (дата, лист, было, стало, кто решил, подпись), работы в этом месте не начинают. 3. Затронуты несущая стена, стояк, вентканал или мокрая зона — сразу владельцу раздела и ГИПу (главному инженеру проекта); между разделами не больше двух кругов, затем решает ГИП. 4. На объекте устно ничего не согласуется: каждое решение — записью в реестр с подписью.

Этап 1. До демонтажа

№	Где	Способ	Что сделать	Кто выполняет	Точность	Что пересчитается в альбоме	Чем подтверждается	Закрывает вопросы реестра
О-1	Ввод В1 и Т3 у стояков; по всей квартире	Обмер	Отключающая арматура и счётчики воды на вводах: положение, тип, пломбы управляющей компании. Альбом ставит их на каждом вводе по практике, в данных их нет.	Архитектор	±5 мм	Узлы ввода в спецификации ВК (краны, фильтры, счётчики); места ввода на плане выводов. Листы: л. 49, 50 — План выводов сантехники л. 53 — Спецификация сантехнического оборудования	акт контрольного обмера; фото с рулеткой и привязкой к стене или углу	Вопроса в реестре нет: Альбом принимает счётчики воды на вводах без осмотра. Результат принимает: Инженер ВК (вода, канализация)
О-2	Вход в квартиру или лестничная клетка; место щита на плане	Обмер	Существующий щиток и счётчик электроэнергии: место и габарит ниши, состояние ввода, марка и сечение вводного кабеля, наличие вводного автомата и УЗО, пломбы.	Архитектор	±5 мм	Ниша и место щита на листах; вводной кабель и аппараты на однолинейной схеме; расстояния до первых групп. Листы: л. 39, 40 — Однолинейная схема щита	акт контрольного обмера; фото с рулеткой и привязкой к стене или углу	Вопроса в реестре нет: Альбом принимает щит и ввод без осмотра. Результат принимает: Инженер-электрик
О-3	Кухня-столовая (пом. 1), Кабинет-гостевая (пом. 2), Гостиная (пом. 5), Спальня мастер (пом. 13), Спальня 2 (пом. 16), Спальня 3 (пом. 18), Спальня 4 (пом. 19); у окон	Обмер	Положение стояков отопления (подающий и обратный) от граней стен, диаметры, наличие запорной арматуры; существующие радиаторы: число секций, межосевое расстояние, подводки. В данных стояков отопления нет — лист отопления выводит их условно у откоса окна, радиаторы — «принципиально, по расчёту».	Архитектор	±5 мм	План отопления: места стояков и подводок, привязки радиаторов; подбор радиаторов по теплотехническому расчёту; радиаторы и узлы подключения в ВОР и спецификации. Листы: л. 47, 48 — План отопления	акт контрольного обмера; фото с рулеткой и привязкой к стене или углу	Вопроса в реестре нет: Альбом принимает положение стояков и радиаторов отопления без обмера. Результат принимает: Инженер ОВ
О-4	все помещения	Обмер	Контрольный обмер всех помещений: стороны, диагонали, проёмы, высота потолка.	исполнитель	±5 мм; диагонали — разница от 5 мм подписывается	обмерный и монтажный планы, развёртки, мебель на заказ Листы: л. 15, 16 — Обмерный план л. 15, 17, 19, 22, 24, 31, 33, 35, 41, 43, 45, 47, 49, 51, 55, 64, 67, 78, 84, 108–110 — 1-й этаж л. 24, 25 — План расстановки мебели	акт контрольного обмера	К-1 Результат принимает: Архитектор

Допущения и предложения на листе
Основа листа: размеры и контуры этажей подобраны проектировщиком по составу помещений и площадям этажей с картинки 470 px (размеры на ней не читаются); обмер и исходный проект — задание (К-1); высоты: 1-й этаж 2800 мм, мансарда 2700 мм (горизонтальная часть) приняты; скаты кровли мансарды приняты по картинке: колено 1200 мм, уклон 45°, конёк вдоль длинной стороны; проект КР — задание (К-2); наружные стены 400 мм, перегородки 120 мм приняты (К-1); разрешённая мощность 15 кВт принята по типовым ТУ для частного дома (К-4); подрайон климата не задан — принят не северный (жилые от 2,5 м) (К-7).
См. лист открытых вопросов (лист 7, записи К-1, К-2, К-4, К-7).

Изм.	Кол.уч	Лист	№ док.	Подп.	Дата
Разраб.		Кырлан А.С.			21.10.26
Пров.					
ГИП					
Н. контр.					
Утв.					

ГД-2026-010-АИ

Дом 331 м²

Общая площадь 270,67* м² · * размеры приняты, не замерены (реестр — л. 7, К-1)

Дизайн-проект интерьера

Стадия	Лист	Листов
РП	8	159

Задание на контрольный обмер и обследование.
Лист 1 из 3
М б/м

Кырлан Александр Сергеевич

выпуск 18.10.2026 № 9365d64cec · стр. 10 из 197

Задание на контрольный обмер и обследование. Лист 2 из 3

Что замерить, вскрыть и получить до заказа материалов и изделий

Этап 1. До демонтажа (продолжение)

№	Где	Способ	Что сделать	Кто выполняет	Точность	Что пересчитается в альбоме	Чем подтверждается	Закрывает вопросы реестра
О-5	Все помещения квартиры	Обмер	Высота потолка в каждом помещении в нескольких точках: центр, углы, у проёмов.	Архитектор	±5 мм	Вертикальные размеры альбома: развёртки, шкафы, плитка, объёмы работ. Листы: л. 2–6 — Общие данные	акт контрольного обмера	К-2 Результат принимает: Архитектор
О-6	холл с лестницей / холл мансарды	Обмер	Разность отметок чистых полов 1-го этажа и мансарды, толщина перекрытия, положение и размеры проёма над маршем (по проекту КР или по факту).	исполнитель		лист «Лестница Л-1*», планы этажей, ведомость ограждений Листы: architect/stairs-л-1 (лист по названию не найден)		К-6 Результат принимает: Архитектор
О-7	По месту	Обмер	Подтвердить на объекте принятое: подрайон климата не задан — принят не северный (жилые от 2,5 м)	Архитектор	±5 мм	Листы, где используется принятая величина. Листы: л. 2–6 — Общие данные	акт контрольного обмера	К-7 Результат принимает: Архитектор

Этап 2. После демонтажа, до черновых работ

№	Где	Способ	Что сделать	Кто выполняет	Точность	Что пересчитается в альбоме	Чем подтверждается	Закрывает вопросы реестра
О-8	Кухня-столовая (пом. 1), Кабинет-гостевая (пом. 2), Санузел 1 этажа (пом. 3), Котельная (пом. 4), Гостиная (пом. 5), Холл с лестницей (пом. 6), Кладовая (пом. 7), Прихожая (пом. 8), Тамбур (пом. 9), Гараж (пом. 10), Веранда (пом. 11), Крыльцо (пом. 12), Спальня мастер (пом. 13), Гардеробная мастер (пом. 14), Санузел мастер (пом. 15), Спальня 2 (пом. 16), Холл мансарды (пом. 17), Спальня 3 (пом. 18), Спальня 4 (пом. 19), Санузел 2 (пом. 20)	Обмер	Нивелировка плиты перекрытия и существующего пола после демонтажа покрытий: отметки в углах и по сетке, перепады по помещению, уклоны, отметки порогов (чистый пол в мокрых зонах принят -30 мм, -15 мм, 0 мм). Принятая толщина стяжки 33 мм, 50 мм, 53 мм, 55 мм, 61 мм и отметка чистого пола расчётные, не от замера плиты.	Архитектор	±5 мм по отметке; ровность просвет под 2-метровой рейкой, горизонталь против 0,2 % длины помещения	Толщина стяжки и отметка чистого пола; уклоны к трапам и пороги; выпуски К1 относительно чистого пола (план разводки); объёмы стяжки и смеси в ВОР и спецификации. Листы: л. 61, 67–69 — План полов л. 51, 52 — Схема разводки водопровода и канализации	акт контрольного обмера	Вопроса в реестре нет: Альбом принимает отметки плиты и толщину пирога пола без нивелировки. Результат принимает: Отделочник
О-9	Кухня-столовая (пом. 1), Кабинет-гостевая (пом. 2), Санузел 1 этажа (пом. 3), Котельная (пом. 4), Гостиная (пом. 5), Холл с лестницей (пом. 6), Кладовая (пом. 7), Прихожая (пом. 8), Тамбур (пом. 9), Гараж (пом. 10), Веранда (пом. 11), Крыльцо (пом. 12), Спальня мастер (пом. 13), Гардеробная мастер (пом. 14), Санузел мастер (пом. 15), Спальня 2 (пом. 16), Холл мансарды (пом. 17), Спальня 3 (пом. 18), Спальня 4 (пом. 19), Санузел 2 (пом. 20)	Обмер	Вертикаль и плоскостность стен: отклонение от вертикали по высоте стены (отвес или лазерный уровень), просвет под правилом 2 м, кривизна углов. Нужно там, где от стены зависит изделие: облицовка плиткой (пом. 3, 15, 20), штукатурка и окраска (пом. 1, 2, 3, 4, 5, 6, 7, 8, 9, 10, 11, 12, 13, 14, 15, 16, 17, 18, 19, 20), встроенная мебель и кухня (пом. 1, 8, 16, 18, 19).	Архитектор	до 1 мм на 2 м (правило и клиновой щуп); вертикаль — мм на высоту стены, отклонения подписываются на плане	Толщина штукатурки и расход смеси в ВОР и спецификации; раскладка плитки (подрезка у стен); зазоры и крепление встроенной мебели и кухни. Листы: л. 61–66 — Раскладка плитки л. 70–72 — Ведомость отделки помещений	акт контрольного обмера	Вопроса в реестре нет: Альбом принимает стены ровными и вертикальными без замера. Результат принимает: Отделочник

Допущения и предложения на листе

Основа листа: размеры и контуры этажей подобраны проектировщиком по составу помещений и площадям этажей с картинки 470 px (размеры на ней не читаются); обмер и исходный проект — задание (К-1); высоты: 1-й этаж 2800 мм, мансарда 2700 мм (горизонтальная часть) приняты; скаты кровли мансарды приняты по картинке: колено 1200 мм, уклон 45°, конёк вдоль длинной стороны; проект КР — задание (К-2); наружные стены 400 мм, перегородки 120 мм приняты (К-1); разрешённая мощность 15 кВт принята по типовым ТУ для частного дома (К-4); подрайон климата не задан — принят не северный (жилые от 2,5 м) (К-7).

Знак «*» — принято, не замерено и не подтверждено (замерить на объекте): К-6: Л-1 — габарит марша снят с картинки заказчика (11 проступей в холле 3,6 м), а до отм. +3,150 нужно 18 подъёмов — одномаршевая не встаёт: решение по К-6.

См. лист открытых вопросов (лист 7, записи К-1, К-2, К-4, К-6, К-7).

Изм.	Кол.уч	Лист	№ док.	Подп.	Дата
Разраб.		Кырлан А.С.			21.10.26
Пров.					
ГИП					
Н. контр.					
Утв.					

ГД-2026-010-АИ

Дом 331 м²

Общая площадь 270,67* м² · * размеры приняты, не замерены (реестр — л. 7, К-1)

Дизайн-проект интерьера

Стадия	Лист	Листов
РП	9	159

Задание на контрольный обмер и обследование.
Лист 2 из 3
М б/м

Кырлан Александр Сергеевич

выпуск 18.10.2026 № 9365d64cec · стр. 11 из 197

Задание на контрольный обмер и обследование. Лист 3 из 3

ПРЕДВАРИТЕЛЬНО · не для производства работ · открыто пунктов: 6 (реестр — л. 7)

Что замерить, вскрыть и получить до заказа материалов и изделий

Документы и данные закупки (не на объекте)

№	У кого, откуда	Способ	Что получить	К какому сроку	Что пересчитается в альбоме	Чем подтверждается	Закрывает вопросы реестра
О-10	Заказчик; организация, выдавшая технические условия	Документ	Технические условия на присоединение: разрешённая мощность.	До утверждения однолинейной схемы щита	Однолинейная схема щита: вводной аппарат и группы. Листы: л. 2–6 — Общие данные	копия документа	К-4 Результат принимает: Инженер-электрик
О-11	вся квартира	Документ	Поэтажный план БТИ и техническое заключение о несущих стенах.	до демонтажа и возведения перегородок	монтажный план, проёмы, развёртки Листы: л. 15, 16 — Обмерный план л. 15, 17, 19, 22, 24, 31, 33, 35, 41, 43, 45, 47, 49, 51, 55, 64, 67, 78, 84, 108–110 — 1-й этаж	копия документа	К-5 Результат принимает: Архитектор
О-12	адрес объекта, СП 131.13330	Документ	Климатический подрайон по СП 131.13330 (по адресу объекта)	до заказа каркаса потолков	план потолков, разрезы, ведомость объёмов Листы: л. 55, 56 — План потолков л. 15, 17, 19, 22, 24, 31, 33, 35, 41, 43, 45, 47, 49, 51, 55, 64, 67, 78, 84, 108–110 — 1-й этаж	копия документа	К-7 Результат принимает: Архитектор

Примечания

1. Подтверждение: акт контрольного обмера (дата, кто присутствовал, прибор, перечень промеров с результатами, подписи присутствующих); к акту — фото вскрытий и узлов и техническое заключение организации, выполнившей обследование.
2. Номера листов — по ведомости рабочих чертежей комплекта (лист «Общие данные»).
3. Пункт исключается из задания при следующем выпуске, когда акт подписан, значение внесено в проект и листы перевыпущены; знак «*» у величины снимается только замером.

Допущения и предложения на листе

Основа листа: размеры и контуры этажей подобраны проектировщиком по составу помещений и площадям этажей с картинки 470 px (размеры на ней не читаются); обмер и исходный проект — задание (К-1); высоты: 1-й этаж 2800 мм, мансарда 2700 мм (горизонтальная часть) приняты; скаты кровли мансарды приняты по картинке: колено 1200 мм, уклон 45°, конёк вдоль длинной стороны; проект КР — задание (К-2); наружные стены 400 мм, перегородки 120 мм приняты (К-1); разрешённая мощность 15 кВт принята по типовым ТУ для частного дома (К-4); подрайон климата не задан — принят не северный (жилые от 2,5 м) (К-7).

См. лист открытых вопросов (лист 7, записи К-1, К-2, К-4, К-7).

Изм.	Кол.уч	Лист	№ док.	Подп.	Дата
Разраб.		Кырлан А.С.			21.10.26
Пров.					
ГИП					
Н. контр.					
Утв.					

ГД-2026-010-АИ

Дом 331 м²

Общая площадь 270,67* м² · * размеры приняты, не замерены (реестр — л. 7, К-1)

Дизайн-проект интерьера

Стадия	Лист	Листов
РП	10	159

Задание на контрольный обмер и обследование.
Лист 3 из 3
М б/м

Кырлан Александр Сергеевич

выпуск 18.10.2026 № 9365d64cec · стр. 12 из 197

График закупок и работ. Лист 1 из 4

Что заказывать и когда не раньше чего: относительный порядок без дат; срок поставки — из данных или «уточняется у поставщика»

Лист не содержит дат: контрольного обмера, подписанных решений автора и договоров ещё нет, и любая дата была бы выдумана. Вместо календаря — порядок и условия: замер → решение и выбор изделия → заказ → срок поставки → работа, которую позиция блокирует. Срок поставки печатается как срок, только если он задан в данных позиции. Нет — «срок уточняется у поставщика» и ссылка на вопрос реестра о сроках; типовой диапазон практики стоит рядом как ориентир и заказывать по нему нельзя. Номера З-N и Р-N — строки этого листа, К-N — записи реестра открытых вопросов, О-N — позиции задания на контрольный обмер.

Закупки: что заказывается, от чего зависит заказ и какую работу блокирует

№	Позиция и где	1. Замер до заказа	2. Решение, выбор изделия, паспорт	3. Условие заказа	4. Срок поставки	5. Блокирует работу	Закрывает вопросы реестра
З-1	Двери скрытого монтажа с коробом под покраску в существующих проёмах: Д-1, Д-2, Д-7, Д-8, Д-9, Д-10, Д-11, Д-12, Д-13 — 9 шт. пом. 2, 3, 13, 14, 15, 16, 18, 19, 20	О-4: обмер: все помещения (К-1); до заказа мебели и дверей		После 1 и 2 и после получения срока у поставщика (вопроса о сроках нет); дата заказа — когда срок известен, не позднее чем за срок до начала Р-5.	срок уточняется у поставщика Ориентир практики (не срок поставщика): ≈ 30 дн.	Р-5 «штукатурка»: короб ставят до штукатурки (коробку ставят на черновой стадии; полотно навешивают после чистовой отделки стен)	К-1
З-2	Кухонный гарнитур по проекту кухни: модули Кх1, Кх2, Кх4, Кх3, Кх5, Кх6, Кх10, Кх11, Кх12, Кх13 пом. 1			После 1 и 2 и после получения срока у поставщика (вопроса о сроках нет); дата заказа — когда срок известен, не позднее чем за срок до начала Р-15.	срок уточняется у поставщика Ориентир практики (не срок поставщика): 4–8 нед. от замера	Р-15 «кухня и мебель»: замер кухни — по готовым стенам после штукатурки или плитки, до чистового пола; производство идёт параллельно со стяжкой и отделкой	
З-3	Встраиваемая техника кухни: Кх2 посудомоечная машина, Кх5 холодильник пом. 1			После 1 и 2 и после получения срока у поставщика (вопроса о сроках нет); дата заказа — когда срок известен, не позднее чем за срок до начала Р-15.	срок уточняется у поставщика	Р-15 «кухня и мебель»: паспорта и монтажные схемы — до изготовления модулей кухни: нишу и вентзазоры задаёт модель, а не типовая схема 60 см	
З-4	Стиральная машина: Сд4 (вертикальная загрузка 400 × 600 мм — условие закупки) пом. 20			После 1 и 2 и после получения срока у поставщика (вопроса о сроках нет); дата заказа — когда срок известен, не позднее чем за срок до начала Р-4.	срок уточняется у поставщика	Р-4 «черновая сантехника»: габарит и подводка — до закрытия люка и разводки	
З-5	Сантехнические приборы и инсталляции: Сн1, Сн2, Сн3, См1, См2, См3, Сд1, Сд2, Сд3 пом. 3, 15, 20	О-3: обмер: Кухня-столовая (пом. 1), Кабинет-гостевая (пом. 2), Гостиная (пом. 5), Спальня мастер (пом. 13), Спальня 2 (пом. 16), Спальня 3 (пом. 18), Спальня 4 (пом. 19); у окон		После 1 и 2 и после получения срока у поставщика (вопроса о сроках нет); дата заказа — когда срок известен, не позднее чем за срок до начала Р-4.	срок уточняется у поставщика	Р-4 «черновая сантехника»: инсталляцию ставят до обшивки ГКЛВ и до гидроизоляции стены	

Допущения и предложения на листе

Основа листа: размеры и контуры этажей подобраны проектировщиком по составу помещений и площадям этажей с картинки 470 px (размеры на ней не читаются); обмер и исходный проект — задание (К-1); высоты: 1-й этаж 2800 мм, мансарда 2700 мм (горизонтальная часть) приняты; скаты кровли мансарды приняты по картинке: колено 1200 мм, уклон 45°, конёк вдоль длинной стороны; проект КР — задание (К-2); наружные стены 400 мм, перегородки 120 мм приняты (К-1); разрешённая мощность 15 кВт принята по типовым ТУ для частного дома (К-4); подрайон климата не задан — принят не северный (жилые от 2,5 м) (К-7).

См. лист открытых вопросов (лист 7, записи К-1, К-2, К-4, К-7).

Изм.	Кол.уч	Лист	№ док.	Подп.	Дата
Разраб.		Кырлан А.С.			21.10.26
Пров.					
ГИП					
Н. контр.					
Утв.					

ГД-2026-010-АИ

Дом 331 м²

Общая площадь 270,67* м² · * размеры приняты, не замерены (реестр — л. 7, К-1)

Дизайн-проект интерьера

Стадия	Лист	Листов
РП	11	159

График закупок и работ. Лист 1 из 4

М б/м

Кырлан Александр Сергеевич

выпуск 18.10.2026 № 9365d64cec · стр. 13 из 197

График закупок и работ. Лист 2 из 4

Что заказывать и когда не раньше чего: относительный порядок без дат; срок поставки — из данных или «уточняется у поставщика»

Закупки: что заказывается, от чего зависит заказ и какую работу блокирует (продолжение)

№	Позиция и где	1. Замер до заказа	2. Решение, выбор изделия, паспорт	3. Условие заказа	4. Срок поставки	5. Блокирует работу	Закрывает вопросы реестра
З-6	Керамогранит и плитка: 3 поз. по артикулу и формату, 126,65 м² по раскладке пом. 3, 4, 8, 9, 11, 12, 15, 20	О-8: обмер: Кухня-столовая (пом. 1), Кабинет-гостевая (пом. 2), Санузел 1 этажа (пом. 3), Котельная (пом. 4), Гостиная (пом. 5), Холл с лестницей (пом. 6), Кладовая (пом. 7), Прихожая (пом. 8), Тамбур (пом. 9), Гараж (пом. 10), Веранда (пом. 11), Крыльцо (пом. 12), Спальня мастер (пом. 13), Гардеробная мастер (пом. 14), Санузел мастер (пом. 15), Спальня 2 (пом. 16), Холл мансарды (пом. 17), Спальня 3 (пом. 18), Спальня 4 (пом. 19), Санузел 2 (пом. 20) О-9: обмер: Кухня-столовая (пом. 1), Кабинет-гостевая (пом. 2), Санузел 1 этажа (пом. 3), Котельная (пом. 4), Гостиная (пом. 5), Холл с лестницей (пом. 6), Кладовая (пом. 7), Прихожая (пом. 8), Тамбур (пом. 9), Гараж (пом. 10), Веранда (пом. 11), Крыльцо (пом. 12), Спальня мастер (пом. 13), Гардеробная мастер (пом. 14), Санузел мастер (пом. 15), Спальня 2 (пом. 16), Холл мансарды (пом. 17), Спальня 3 (пом. 18), Спальня 4 (пом. 19), Санузел 2 (пом. 20)		После 1 и 2 и после получения срока у поставщика (вопроса о сроках нет); дата заказа — когда срок известен, не позднее чем за срок до начала Р-9.	срок уточняется у поставщика	Р-9 «плитка»: калибр партии измеряют до раскладки, раскладку пересчитывают до заказа	
З-7	Покрытие пола (доска) и плинтус: пом. 1, 2, 5, 6, 7, 13, 14, 16, 17, 18, 19 пом. 1, 2, 5, 6, 7, 13, 14, 16, 17, 18, 19	О-8: обмер: Кухня-столовая (пом. 1), Кабинет-гостевая (пом. 2), Санузел 1 этажа (пом. 3), Котельная (пом. 4), Гостиная (пом. 5), Холл с лестницей (пом. 6), Кладовая (пом. 7), Прихожая (пом. 8), Тамбур (пом. 9), Гараж (пом. 10), Веранда (пом. 11), Крыльцо (пом. 12), Спальня мастер (пом. 13), Гардеробная мастер (пом. 14), Санузел мастер (пом. 15), Спальня 2 (пом. 16), Холл мансарды (пом. 17), Спальня 3 (пом. 18), Спальня 4 (пом. 19), Санузел 2 (пом. 20)		После 1 и 2 и после получения срока у поставщика (вопроса о сроках нет); дата заказа — когда срок известен, не позднее чем за срок до начала Р-12.	срок уточняется у поставщика	Р-12 «чистовые полы»: артикул и партия — до заказа; доску привозят к чистовым полам	
З-8	Встроенная мебель по замеру цеха: Пр1, С3, Д3, Д6 пом. 8, 16, 18, 19	О-4: обмер: все помещения (К-1); до заказа мебели и дверей		После 1 и 2 и после получения срока у поставщика (вопроса о сроках нет); дата заказа — когда срок известен, не позднее чем за срок до начала Р-15.	срок уточняется у поставщика Ориентир практики (не срок поставщика): 4–8 нед. от замера	Р-15 «кухня и мебель»: цех замеряет по готовым стенам; производство 4–8 недель идёт параллельно с отделкой	К-1

Допущения и предложения на листе

Основа листа: размеры и контуры этажей подобраны проектировщиком по составу помещений и площадям этажей с картинки 470 px (размеры на ней не читаются); обмер и исходный проект — задание (К-1); высоты: 1-й этаж 2800 мм, мансарда 2700 мм (горизонтальная часть) приняты; скаты кровли мансарды приняты по картинке: колено 1200 мм, уклон 45°, конёк вдоль длинной стороны; проект КР — задание (К-2); наружные стены 400 мм, перегородки 120 мм приняты (К-1); разрешённая мощность 15 кВт принята по типовым ТУ для частного дома (К-4); подрайон климата не задан — принят не северный (жилые от 2,5 м) (К-7).

См. лист открытых вопросов (лист 7, записи К-1, К-2, К-4, К-7).

Изм.	Кол.уч	Лист	№ док.	Подп.	Дата
Разраб.		Кырлан А.С.			21.10.26
Пров.					
ГИП					
Н. контр.					
Утв.					

ГД-2026-010-АИ

Дом 331 м²

Общая площадь 270,67* м² · * размеры приняты, не замерены (реестр — л. 7, К-1)

	Стадия	Лист	Листов
Дизайн-проект интерьера	РП	12	159

График закупок и работ. Лист 2 из 4

М б/м

Кырлан Александр Сергеевич

выпуск 18.10.2026 № 9365d64cec · стр. 14 из 197

График закупок и работ. Лист 3 из 4

Что заказывать и когда не раньше чего: относительный порядок без дат; срок поставки — из данных или «уточняется у поставщика»

Работы: порядок и что не даёт начать

№	Работа (стадия технологической последовательности)	После	Что должно быть к началу: условия и закупки	Не начинать, пока открыто в реестре
Р-1	Демонтаж покрытий, отделки стен и потолков, дверных блоков и приборов; конструкции, стены и перегородки не трогать до технического заключения (стадия 1)		до начала: запрошены документы на дом и БТИ; контрольный обмер до демонтажа (что видно) сделан	
Р-2	Контрольный обмер на голых стенах и обследование (задание — лист «Задание на контрольный обмер») (стадия 2)	Р-1	после снятия отделки: видны стояки, каналы, щиток, толщины стен; до заказа всего, что делают по размеру	
Р-3	Черновая электрика: штробы, короба, гофра, подрозетники, щит (стадия 4)	Р-2	до начала: план электрики с высотами утверждён; штробы в стенах — только после технического заключения; мебель расставлена	К-4: Разрешённая мощность дома по ТУ неизвестна, принята 15 кВт.
Р-4	Черновая сантехника и вентиляция: разводка, выводы, инсталляции, короба стояков (стадия 5)	Р-2	до начала: положение стояков замерено; модели инсталляций и машины выбраны (габариты рамы, подводка); инсталляцию ставят до обшивки ГКЛВ и до гидроизоляции Закупки к началу: 3-4 (стиральная машина), 3-5 (сантехника)	
Р-5	Коробки скрытых дверей, затем штукатурка стен и откосов (стадия 6)	Р-2, Р-3, Р-4	до начала: электрика и сантехника смонтированы, штробы заделаны; коробки скрытых дверей установлены до штукатурки (поэтому заказ дверей — раньше работы) Закупки к началу: 3-1 (двери скрытого монтажа)	К-1: Размеры дома на картинке заказчика (470 px) не читаются: состав помещений и форма сняты с картинки, размеры подобраны проектировщиком под площади этажей 185,80 и 145,73 м².
Р-6	Стяжка пола и тёплый пол (стадия 7)	Р-5	до начала: штукатурка сделана; трубы под стяжкой приняты; нивелировка плиты выполнена	
Р-7	Гидроизоляция санузлов и тест проливом (стадия 8)	Р-6	до начала: стяжка набрала прочность и сухая по инструкции гидроизоляции; выводы стоят на проектных отметках	
Р-8	ГКЛ: короба инсталляции и стояков, ниши, потолки (стадия 9)	Р-3, Р-4	до начала: черновые сети в зоне коробов приняты; закладные под тяжёлое и карнизы стоят; светильники выбраны (вырезы)	
Р-9	Плитка и керамогранит: стены, затем пол; фартук (стадия 10)	Р-6, Р-7, Р-8	до начала: гидроизоляция принята; плитка выбрана, калибр партии измерен, раскладка пересчитана и подписана Закупки к началу: 3-6 (плитка)	
Р-10	Шпаклёвка стен и потолков под окраску (стадия 11)	Р-5, Р-8, Р-9	до начала: плитка готова (грязные работы закончены); штукатурка и ГКЛ сухие	
Р-11	Окраска стен, потолков, откосов (стадия 13)	Р-10	до начала: шпаклёвка отшлифована и огрунтована; выкрасы утверждены, колеровка одной партией	
Р-12	Чистовые полы: инженерная доска (стадия 14)	Р-9, Р-11	до начала: влажность основания в норме, мокрые работы закончены; доска выбрана и привезена Закупки к началу: 3-7 (доска и плинтус)	
Р-13	Полотна межкомнатных дверей, плинтусы, пороги (стадия 15)	Р-11, Р-12	до начала: чистовой пол уложен; полотна скрытых дверей — после чистовой отделки стен	
Р-14	Чистовая электрика и сантехника: механизмы, светильники, смесители, приборы (стадия 16)	Р-11, Р-13	до начала: отделка готова; механизмы, светильники и приборы выбраны и привезены	
Р-15	Кухня, встроенная и корпусная мебель, бытовая техника (стадия 17)	Р-13, Р-14	до начала: чистовая сантехника и электрика подведены к местам мебели; замер кухни снят по готовым стенам (после штукатурки или плитки, до чистового пола) Закупки к началу: 3-2 (кухонный гарнитур), 3-3 (техника кухни), 3-8 (мебель по замеру)	К-1: Размеры дома на картинке заказчика (470 px) не читаются: состав помещений и форма сняты с картинки, размеры подобраны проектировщиком под площади этажей 185,80 и 145,73 м².
Р-16	Сдача: осмотр по чек-листу, дефектная ведомость, устранение замечаний (стадия 18)	Р-14, Р-15	до начала: всё смонтировано; акты скрытых работ подписаны	

Допущения и предложения на листе

Основа листа: размеры и контуры этажей подобраны проектировщиком по составу помещений и площадям этажей с картинки 470 px (размеры на ней не читаются); обмер и исходный проект — задание (К-1); высоты: 1-й этаж 2800 мм, мансарда 2700 мм (горизонтальная часть) приняты; скаты кровли мансарды приняты по картинке: колено 1200 мм, уклон 45°, конёк вдоль длинной стороны; проект КР — задание (К-2); наружные стены 400 мм, перегородки 120 мм приняты (К-1); разрешённая мощность 15 кВт принята по типовым ТУ для частного дома (К-4); подрайон климата не задан — принят не северный (жилые от 2,5 м) (К-7).

См. лист открытых вопросов (лист 7, записи К-1, К-2, К-4, К-7).

Изм.	Кол.уч	Лист	№ док.	Подп.	Дата
Разраб.		Кырлан А.С.			21.10.26
Пров.					
ГИП					
Н. контр.					
Утв.					

ГД-2026-010-АИ

Дом 331 м²

Общая площадь 270,67* м² · * размеры приняты, не замерены (реестр — л. 7, К-1)

Дизайн-проект интерьера

Стадия	Лист	Листов
РП	13	159

График закупок и работ. Лист 3 из 4

М б/м

Кырлан Александр Сергеевич

выпуск 18.10.2026 № 9365d64cec · стр. 15 из 197

График закупок и работ. Лист 4 из 4

Что заказывать и когда не раньше чего: относительный порядок без дат; срок поставки — из данных или «уточняется у поставщика»

Примечания

1. Порядок работ — стадии технологической последовательности из 16 позиций, присутствующих в этом проекте (по строкам ведомости объёмов); остальные стадии таблицы knowledge/remont-tehnologiya.md в проекте не встречаются. Длительности работ не печатаются: их нет ни в данных, ни в нормах для этого объекта.
2. Типовые сроки — ориентир практики, не срок поставщика: скрытые двери — короб около 10 дн., полотно под покраску до 3 нед., шпон 4–5 нед., в среднем около 30 дн. (knowledge/workers/foreman.md, п. 2.4 (profil-doors)); кухня и корпусная мебель — 4–8 недель от замера (knowledge/remont-tehnologiya.md, разд. 2; knowledge/workers/foreman.md, п. 2.4). Заказ по ориентиру не назначается: срок получают у поставщика (вопрос реестра), после чего заказ планируют «не позднее чем за срок до начала работы».
3. Условия заказа берутся из реестра открытых вопросов и задания на контрольный обмер: позиция заказывается, когда закрыты замер (графа 1) и решение (графа 2). Закрывать их может только факт или решение автора с подписью; снять строку с листа можно только закрыв запись реестра.
4. Заказ по размеру до контрольного обмера не делают: двери, кухня и встроенная мебель зависят от обмера (К-11, К-13); скрытые двери, кроме того, зависят от решения по нише санузла 2 (проём Д-5 в перегородке П-1).
5. Номера листов — по ведомости рабочих чертежей комплекта (лист «Общие данные»).

Допущения и предложения на листе

Основа листа: размеры и контуры этажей подобраны проектировщиком по составу помещений и площадям этажей с картинки 470 px (размеры на ней не читаются); обмер и исходный проект — задание (К-1); высоты: 1-й этаж 2800 мм, мансарда 2700 мм (горизонтальная часть) приняты; скаты кровли мансарды приняты по картинке: колено 1200 мм, уклон 45°, конёк вдоль длинной стороны; проект КР — задание (К-2); наружные стены 400 мм, перегородки 120 мм приняты (К-1); разрешённая мощность 15 кВт принята по типовым ТУ для частного дома (К-4); подрайон климата не задан — принят не северный (жилые от 2,5 м) (К-7).

См. лист открытых вопросов (лист 7, записи К-1, К-2, К-4, К-7).

						ГД-2026-010-АИ
						Дом 331 м²
						Общая площадь 270,67* м² · * размеры приняты, не замерены (реестр — л. 7, К-1)
Изм.	Кол.уч	Лист	№ док.	Подп.	Дата	
Разраб.		Кырлан А.С.			21.10.26	Дизайн-проект интерьера
Пров.						Стадия: РП · Лист: 14 · Листов: 159
ГИП						
Н. контр.						**График закупок и работ. Лист 4 из 4**
Утв.						М б/м
						Кырлан Александр Сергеевич

выпуск 18.10.2026 № 9365d64cec · стр. 16 из 197

Обмерный план · 1-й этаж

Существующее положение · размеры в мм · отметки от чистого пола

ПРЕДВАРИТЕЛЬНО · не для производства работ · открыто пунктов: 6 (реестр — л. 7)

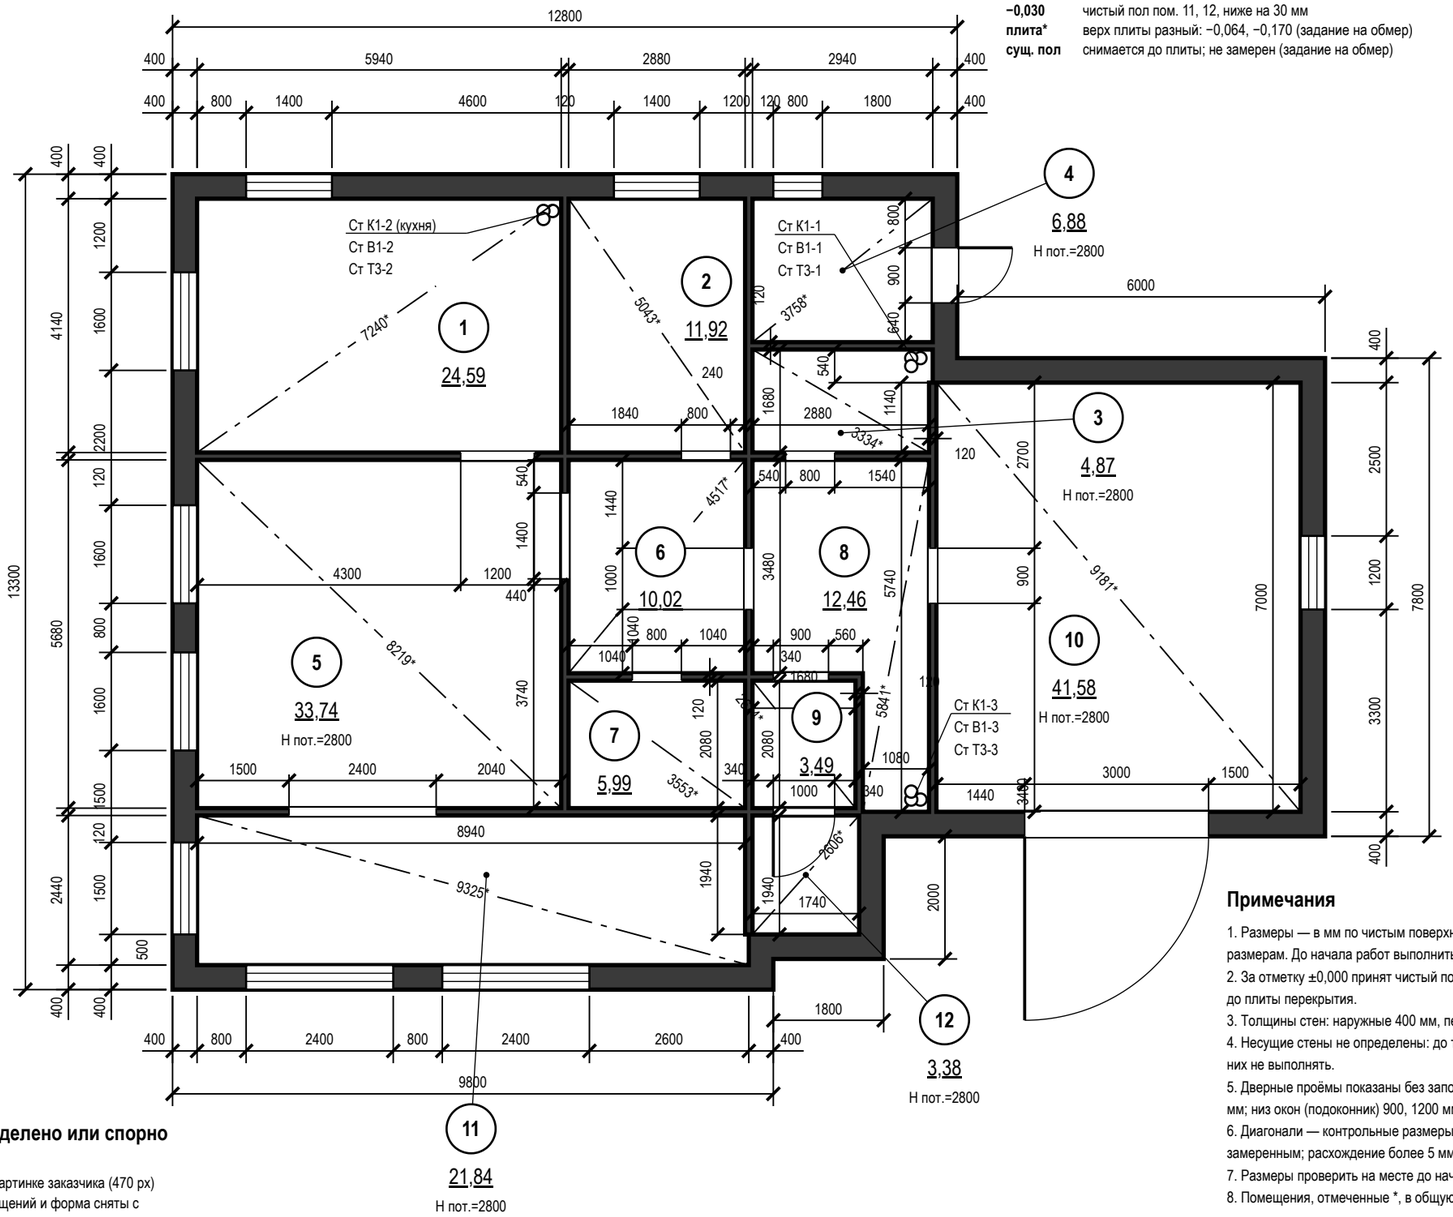

Отметки по высоте

±0,000	чистый пол пом. 1, 2, 4–10; отсчёт высот
−0,015	чистый пол пом. 3, ниже на 15 мм
−0,030	чистый пол пом. 11, 12, ниже на 30 мм
плита*	верх плиты разный: −0,064, −0,170 (задание на обмер)
сущ. пол	снимается до плиты; не замерен (задание на обмер)

Экспликация помещений

№	Наименование	Площадь, м²
1	Кухня-столовая	24,59
2	Кабинет-гостевая	11,92
3	Санузел 1 этажа	4,87
4	Котельная	6,88
5	Гостиная	33,74
6	Холл с лестницей	10,02
7	Кладовая	5,99
8	Прихожая	12,46
9	Тамбур	3,49
10	Гараж	41,58
11	Веранда *	21,84
12	Крыльцо *	3,38
	Итого (общая площадь)	**270,67**

Условные обозначения

- существующие стены (сечение)
- окно (рама, остекление)
- проём существующий, без заполнения (откосы)
- стояк: К1 — канализация, В1 — ХВС, Т3 — ГВС
- диагональ помещения — контроль прямоугольности
- (1) номер помещения, площадь м²

Примечания

1. Размеры — в мм по чистым поверхностям стен до отделки (по плану заказчика); площади — в м² по тем же размерам. До начала работ выполнить контрольный обмер.
2. За отметку ±0,000 принят чистый пол, не существующий (блок отметок). Н пот. — высота от чистого пола до плиты перекрытия.
3. Толщины стен: наружные 400 мм, перегородки 120 мм; отличающиеся толщины и уступы — размерами на плане.
4. Несущие стены не определены: до технического заключения все стены считать несущими; проёмы и штробы в них не выполнять.
5. Дверные проёмы показаны без заполнения; высота дверных проёмов 2100, 2300 мм, проёмов без двери 2100 мм; низ окон (подоконник) 900, 1200 мм от чистого пола, высота окон 1500, 900, 1600 мм.
6. Диагонали — контрольные размеры; «*» — расчёт по принятому контуру (К-1), при обмере заменить замеренным; расхождение более 5 мм подписать на плане как перекос.
7. Размеры проверить на месте до начала работ; расхождение контрольных проемеров ≤ 2 %.
8. Помещения, отмеченные *, в общую площадь квартиры не входят.

Принято, не определено или спорно

полностью — лист 7

К-1 — Размеры дома на картинке заказчика (470 px) не читаются: состав помещений и форма сняты с картинки, размеры подобраны проектировщиком под площади этажей 185,80 и 145,73 м²

К-2 — Высоты этажей и кровля не известны: приняты 2800 мм (1-й этаж) и 2700 мм (горизонтальная часть потолка мансарды); скаты — двускатная кровля, конёк вдоль длинной стороны, колено 1200 мм, уклон 45° (по перспективе и фасаду с картинки)

К-5 — Планировка этажей — предложение проектировщика по составу помещений с картинки (несущие стены, лестница, перекрытие не известны): нужен проект АР/КР дома

Допущения и предложения на листе

Основа листа: размеры и контуры этажей подобраны проектировщиком по составу помещений и площадям этажей с картинки 470 px (размеры на ней не читаются); обмер и исходный проект — задание (К-1); высоты: 1-й этаж 2800 мм, мансарда 2700 мм (горизонтальная часть) приняты; скаты кровли мансарды приняты по картинке: колено 1200 мм, уклон 45°, конёк вдоль длинной стороны; проект КР — задание (К-2); наружные стены 400 мм, перегородки 120 мм приняты (К-1); разрешённая мощность 15 кВт принята по типовым ТУ для частного дома (К-4); подрайон климата не задан — принят не северный (жилые от 2,5 м) (К-7).

Открытые вопросы и конфликты по листу: К-1, К-2, К-5.

См. лист открытых вопросов (лист 7, записи К-1, К-2, К-4, К-5, К-7).

1000 мм · печать 1:1

Изм.	Кол.уч	Лист	№ док.	Подп.	Дата
Разраб.		Кырлан А.С.			21.10.26
Пров.					
ГИП					
Н. контр.					
Утв.					

ГД-2026-010-АИ

Дом 331 м²

Общая площадь 270,67* м² · * размеры приняты, не замерены (реестр — л. 7, К-1)

Дизайн-проект интерьера

Стадия	Лист	Листов
РП	15	159

Обмерный план · 1-й этаж

М 1:100

Кырлан Александр Сергеевич

выпуск 18.10.2026 № 9365d64cec · стр. 17 из 197

Обмерный план · Мансарда

Существующее положение · размеры в мм · отметки от чистого пола

ПРЕДВАРИТЕЛЬНО · не для производства работ · открыто пунктов: 6 (реестр — л. 7)

Отметки по высоте

±0,000	чистый пол пом. 13, 14, 16–19; отсчёт высот
−0,015	чистый пол пом. 15, 20, ниже на 15 мм
−0,064*	верх плиты — расчёт, не замер (задание на обмер)
сущ. пол	снимается до плиты; не замерен (задание на обмер)

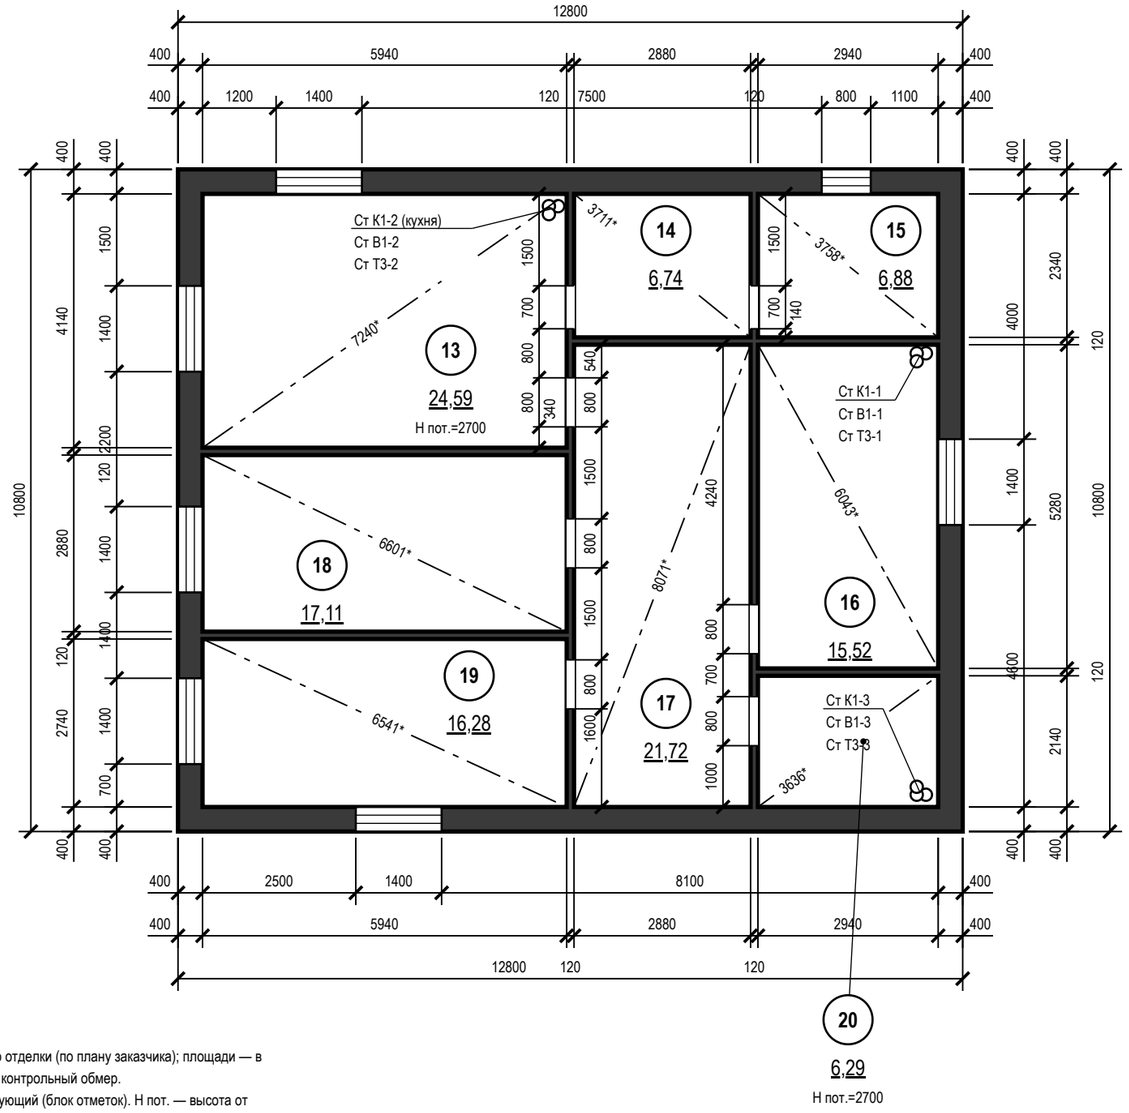

Экспликация помещений

№	Наименование	Площадь, м²
13	Спальня мастер	24,59
14	Гардеробная мастер	6,74
15	Санузел мастер	6,88
16	Спальня 2	15,52
17	Холл мансарды	21,72
18	Спальня 3	17,11
19	Спальня 4	16,28
20	Санузел 2	6,29
	Итого (общая площадь)	**270,67**

Условные обозначения

- существующие стены (сечение)
- окно (рама, остекление)
- проём существующий, без заполнения (откосы)
- стояк: К1 — канализация, В1 — ХВС, Т3 — ГВС
- диагональ помещения — контроль прямоугольности
- (1) номер помещения, площадь м²

Принято, не определено или спорно

полностью — лист 7

К-1 — Размеры дома на картинке заказчика (470 px) не читаются: состав помещений и форма сняты с картинки, размеры подобраны проектировщиком под площади этажей 185,80 и 145,73 м²

К-2 — Высоты этажей и кровля не известны: приняты 2800 мм (1-й этаж) и 2700 мм (горизонтальная часть потолка мансарды); скаты — двускатная кровля, конёк вдоль длинной стороны, колено 1200 мм, уклон 45° (по перспективе и фасаду с картинки)

К-5 — Планировка этажей — предложение проектировщика по составу помещений с картинки (несущие стены, лестница, перекрытие не известны): нужен проект АР/КР дома

Примечания

1. Размеры — в мм по чистым поверхностям стен до отделки (по плану заказчика); площади — в м² по тем же размерам. До начала работ выполнить контрольный обмер.
2. За отметку ±0,000 принят чистый пол, не существующий (блок отметок). Н пот. — высота от чистого пола до плиты перекрытия.
3. Толщины стен: наружные 400 мм, перегородки 120 мм; отличающиеся толщины и уступы размерами на плане.
4. Несущие стены не определены: до технического заключения все стены считать несущими; проёмы и штробы в них не выполнять.
5. Дверные проёмы показаны без заполнения; высота дверных проёмов 2100 мм; низ окон (подоконник) 900, 1500 мм от чистого пола, высота окон 1500, 800 мм.
6. Диагонали — контрольные размеры; «*» — расчёт по принятому контуру (К-1), при обмере заменить замеренным; расхождение более 5 мм подписать на плане как перекос.
7. Размеры проверить на месте до начала работ; расхождение контрольных промеров ≤ 2 %.

Допущения и предложения на листе

Основа листа: размеры и контуры этажей подобраны проектировщиком по составу помещений и площадям этажей с картинки 470 px (размеры на ней не читаются); обмер и исходный проект — задание (К-1); высоты: 1-й этаж 2800 мм, мансарда 2700 мм (горизонтальная часть) приняты; скаты кровли мансарды приняты по картинке: колено 1200 мм, уклон 45°, конёк вдоль длинной стороны; проект КР — задание (К-2); наружные стены 400 мм, перегородки 120 мм приняты (К-1); разрешённая мощность 15 кВт принята по типовым ТУ для частного дома (К-4); подрайон климата не задан — принят не северный (жилые от 2,5 м) (К-7).

Открытые вопросы и конфликты по листу: К-1, К-2, К-5.

См. лист открытых вопросов (лист 7, записи К-1, К-2, К-4, К-5, К-7).

1000 мм · печать 1:1

Изм.	Кол.уч	Лист	№ док.	Подп.	Дата
Разраб.		Кырлан А.С.			21.10.26
Пров.					
ГИП					
Н. контр.					
Утв.					

ГД-2026-010-АИ

Дом 331 м²

Общая площадь 270,67* м² · * размеры приняты, не замерены (реестр — л. 7, К-1)

Дизайн-проект интерьера

Стадия	Лист	Листов
РП	16	159

Обмерный план · Мансарда

М 1:100

Кырлан Александр Сергеевич

выпуск 18.10.2026 № 9365d64cec · стр. 18 из 197

План демонтажа и монтажа перегородок · 1-й этаж

Перепланировка не выполняется · существующие стены сохраняются · размеры в мм

ПРЕДВАРИТЕЛЬНО · не для производства работ · открыто пунктов: 6 (реестр — л. 7)

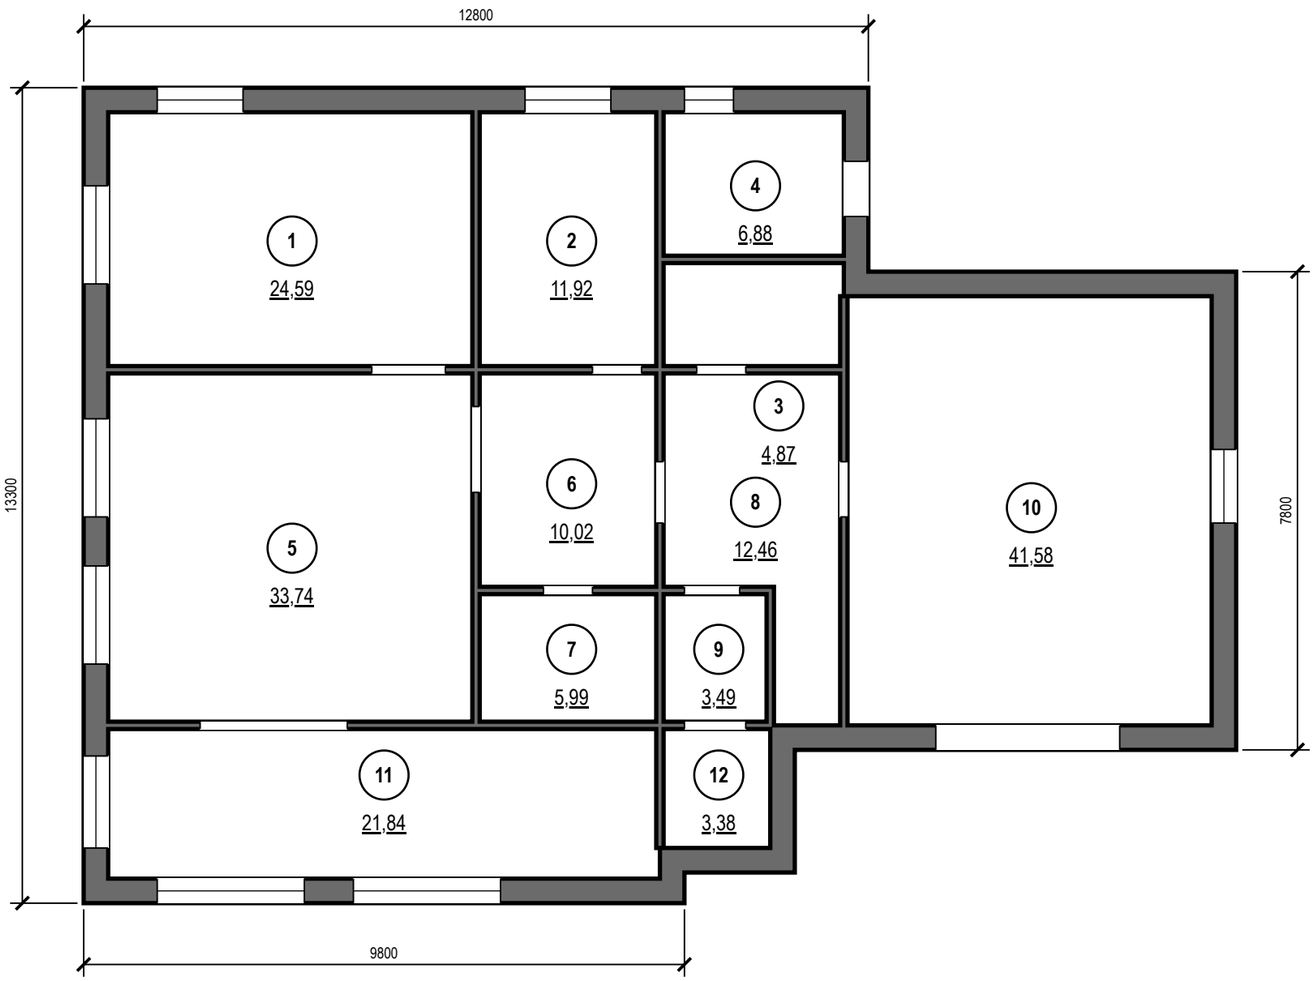

Условные обозначения

- существующие стены — сохраняются;
- несущие не определены — считать несущими
- демонтируемые конструкции — на плане нет
- возводимые перегородки — на плане нет
- проём существующий, без заполнения (откосы)
- (1) номер помещения, площадь м²

Отметки по высоте

±0,000	чистый пол пом. 1, 2, 4–10; отсчёт высот	**плита***	верх плиты разный: −0,064, −0,170 (задание на обмер)
−0,015	чистый пол пом. 3, ниже на 15 мм	**сущ. пол**	снимается до плиты; не замерен (задание на обмер)
−0,030	чистый пол пом. 11, 12, ниже на 30 мм		

Примечания

1. Перепланировка не выполняется: несущие и ненесущие стены, перегородки и плиты перекрытия не демонтируются, новые стены не возводятся; существующие стены и перегородки сохраняются.
2. Дверные блоки — по плану дверей; существующие проёмы не расширяются.
3. Демонтаж существующих покрытий пола, стен и потолка, дверных блоков и сантехприборов (если есть) — до основания; объёмы демонтажа — для справки, по факту на объекте.
4. За отметку ±0,000 принят чистый пол, не существующий (блок отметок). Размеры — в мм по чистовой поверхности стен до отделки.
5. Размеры проверить на месте до начала работ: расхождение с обмером — не более 2 % (иначе — к архитектору).
6. Несущие стены не определены: до технического заключения все стены считать несущими — проёмы, ниши и штробы в них не выполнять.

Допущения и предложения на листе

Основа листа: размеры и контуры этажей подобраны проектировщиком по составу помещений и площадям этажей с картинки 470 px (размеры на ней не читаются); обмер и исходный проект — задание (К-1); высоты: 1-й этаж 2800 мм, мансарда 2700 мм (горизонтальная часть) приняты; скаты кровли мансарды приняты по картинке: колено 1200 мм, уклон 45°, конёк вдоль длинной стороны; проект КР — задание (К-2); наружные стены 400 мм, перегородки 120 мм приняты (К-1); разрешённая мощность 15 кВт принята по типовым ТУ для частного дома (К-4); подрайон климата не задан — принят не северный (жилые от 2,5 м) (К-7).

См. лист открытых вопросов (лист 7, записи К-1, К-2, К-4, К-7).

1000 мм · печать 1:1

Изм.	Кол.уч	Лист	№ док.	Подп.	Дата
Разраб.		Кырлан А.С.			21.10.26
Пров.					
ГИП					
Н. контр.					
Утв.					

ГД-2026-010-АИ

Дом 331 м²

Общая площадь 270,67* м² · * размеры приняты, не замерены (реестр — л. 7, К-1)

Дизайн-проект интерьера

Стадия	Лист	Листов
РП	17	159

План демонтажа и монтажа перегородок · 1-й этаж

М 1:100

Кырлан Александр Сергеевич

выпуск 18.10.2026 № 9365d64cec · стр. 19 из 197

План демонтажа и монтажа перегородок · Мансарда

Перепланировка не выполняется · существующие стены сохраняются · размеры в мм

ПРЕДВАРИТЕЛЬНО · не для производства работ · открыто пунктов: 6 (реестр — л. 7)

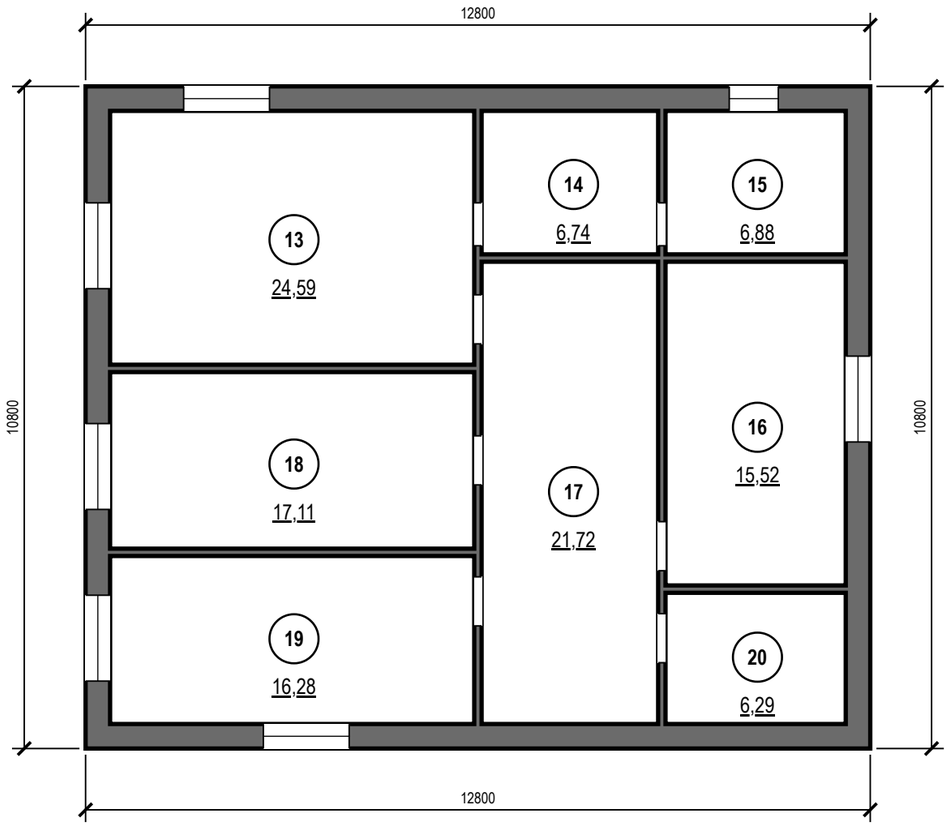

Условные обозначения

- существующие стены — сохраняются; несущие не определены — считать несущими
- демонтируемые конструкции — на плане нет
- возводимые перегородки — на плане нет
- проём существующий, без заполнения (откосы)
- (1) номер помещения, площадь м²

Отметки по высоте

±0,000	чистый пол пом. 13, 14, 16–19; отсчёт высот	**−0,064***	верх плиты — расчёт, не замер (задание на обмер)
−0,015	чистый пол пом. 15, 20, ниже на 15 мм	**сущ. пол**	снимается до плиты; не замерен (задание на обмер)

Примечания

1. Перепланировка не выполняется: несущие и ненесущие стены, перегородки и плиты перекрытия не демонтируются, новые стены не возводятся; существующие стены и перегородки сохраняются.
2. Дверные блоки — по плану дверей; существующие проёмы не расширяются.
3. Демонтаж существующих покрытий пола, стен и потолка, дверных блоков и сантехприборов (если есть) — до основания; объёмы демонтажа — для справки, по факту на объекте.
4. За отметку ±0,000 принят чистый пол, не существующий (блок отметок). Размеры — в мм по чистовой поверхности стен до отделки.
5. Размеры проверить на месте до начала работ: расхождение с обмером — не более 2 % (иначе — к архитектору).
6. Несущие стены не определены: до технического заключения все стены считать несущими — проёмы, ниши и штробы в них не выполнять.

Допущения и предложения на листе

Основа листа: размеры и контуры этажей подобраны проектировщиком по составу помещений и площадям этажей с картинки 470 px (размеры на ней не читаются); обмер и исходный проект — задание (К-1); высоты: 1-й этаж 2800 мм, мансарда 2700 мм (горизонтальная часть) приняты; скаты кровли мансарды приняты по картинке: колено 1200 мм, уклон 45°, конёк вдоль длинной стороны; проект КР — задание (К-2); наружные стены 400 мм, перегородки 120 мм приняты (К-1); разрешённая мощность 15 кВт принята по типовым ТУ для частного дома (К-4); подрайон климата не задан — принят не северный (жилые от 2,5 м) (К-7).
См. лист открытых вопросов (лист 7, записи К-1, К-2, К-4, К-7).

1000 мм · печать 1:1

Изм.	Кол.уч	Лист	№ док.	Подп.	Дата
Разраб.		Кырлан А.С.			21.10.26
Пров.					
ГИП					
Н. контр.					
Утв.					

ГД-2026-010-АИ

Дом 331 м²

Общая площадь 270,67* м² · * размеры приняты, не замерены (реестр — л. 7, К-1)

Дизайн-проект интерьера

Стадия	Лист	Листов
РП	18	159

План демонтажа и монтажа перегородок · Мансарда

М 1:100

Кырлан Александр Сергеевич

выпуск 18.10.2026 № 9365d64cec · стр. 20 из 197

План дверей и ведомость заполнения проёмов · 1-й этаж

Проёмы, марки заполнения, привязки · размеры в мм

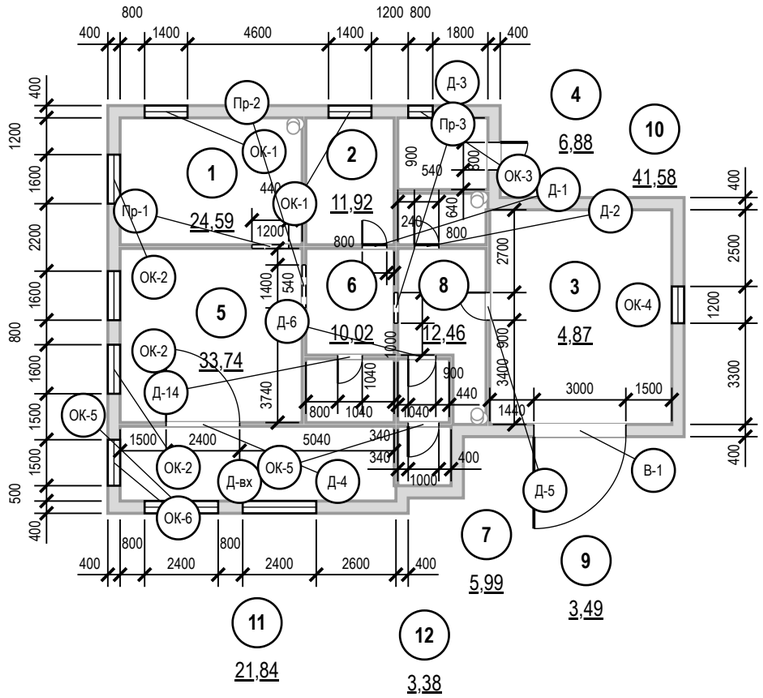

Ведомость заполнения проёмов

Марка	Наименование, обозначение	Проём ш×в, мм	Кол.	Откр.	Отделка полотна	Фурнитура	Прим.
Д-вх	Блок дверной входной, ГОСТ 31173-2016	1000×2100	1	Л	в комплекте блока	в комплекте блока (замки, глазок)	наружу
В-1	Блок дверной входной, ГОСТ 31173-2016	3000×2300	1	Л	в комплекте блока	в комплекте блока (замки, глазок)	наружу
Д-1	Дверь скрытого монтажа, ТУ изготовителя	800×2100	1	П	окраска No. 226 с двух сторон	скрытые петли 3D, магнитный замок	
Д-2	Дверь скрытого монтажа, ТУ изготовителя	800×2100	1	П	в тон облицовки — пом. 3, No. 226 — пом. 8	скрытые петли 3D, магнитный замок, фиксатор WC	порог 15
Д-3	Блок дверной входной, ГОСТ 31173-2016	900×2100	1	П	в комплекте блока	в комплекте блока (замки, глазок)	наружу
Д-4	Блок дверной внутренний, остекл., ГОСТ 475-2016	2400×2100	1	П		петли, ручка с защёлкой	
Д-5	Блок дверной внутренний, ГОСТ 475-2016	900×2100	1	Л		петли, ручка с защёлкой	
Д-6	Блок дверной внутренний, ГОСТ 475-2016	900×2100	1	Л		петли, ручка с защёлкой	
Д-14	Блок дверной внутренний, ГОСТ 475-2016	800×2100	1	Л		петли, ручка с защёлкой	
Пр-1	Портал без заполнения	1200×2100	1				б/п
Пр-2	Портал без заполнения	1400×2100	1				б/п
Пр-3	Портал без заполнения	1000×2100	1				б/п
ОК-1	Блок оконный, ГОСТ 23166-2021	1400×1500	2				низ 900
ОК-2	Блок оконный, ГОСТ 23166-2021	1600×1500	3				низ 900
ОК-3	Блок оконный, ГОСТ 23166-2021	800×900	1				низ 1200
ОК-4	Блок оконный, ГОСТ 23166-2021	1200×900	1				низ 1200
ОК-5	Блок оконный, ГОСТ 23166-2021	2400×1600	2				низ 900
ОК-6	Блок оконный, ГОСТ 23166-2021	1500×1600	1				низ 900

Условные обозначения

- стены (подложка обмера)
- дверь распашная, дуга открывания
- дверь скрытого монтажа
- дверь входная (полотно толще)
- портал (штрих — перемычка)
- оконный блок
- Д — марка типа (Д-N, ПР-N, ОК-N)
- 1 — номер помещения, площадь м²

Допущения и предложения на листе

Основа листа: размеры и контуры этажей подобраны проектировщиком по составу помещений и площадям этажей с картинки 470 px (размеры на ней не читаются); обмер и исходный проект — задание (К-1); высоты: 1-й этаж 2800 мм, мансарда 2700 мм (горизонтальная часть) приняты; скаты кровли мансарды приняты по картинке: колено 1200 мм, уклон 45°, конёк вдоль длинной стороны; проект КР — задание (К-2); наружные стены 400 мм, перегородки 120 мм приняты (К-1); разрешённая мощность 15 кВт принята по типовым ТУ для частного дома (К-4); подрайон климата не задан — принят не северный (жилые от 2,5 м) (К-7).

См. лист открытых вопросов (лист 7, записи К-1, К-2, К-4, К-7).

Примечания

1. Размеры проёмов и привязки — в миллиметрах от чистых граней стен до отделки; привязка — от угла того помещения, со стороны которого стоит размер. Размер в ведомости — ширина × высота проёма от чистого пола 0,000.
2. Марки в кружках — типы заполнения проёмов (ГОСТ 21.501-2018, п. 5.3.2); одна марка — один типоразмер; количество сверено с планом.
3. Открывание: Л — петли слева, П — справа, если смотреть со стороны, куда открывается полотно (на себя).
4. Дверные блоки обычного монтажа (Д-4…Д-6, Д-14) заказывать после чистовой стяжки и штукатурки, проёмы перемерить; монтажный зазор коробки 10–15 мм на сторону, откос от угла помещения до коробки не менее 50 мм.
5. Скрытые двери (Д-1, Д-2): проём замерить в чистоте; блок заказать до штукатурки (≈ 30 дн.), короб ставить до штукатурки; полотно навесить после чистовой отделки, красить в цвет стен. Порядок практика монтажа, изготовитель подтверждает.
6. Размер в ведомости — проёма: полотно скрытой двери уже проёма на коробку и зазор 10–15 мм (модель не выбрана); Д-1, Д-2 — существующие проёмы, до техзаключения не расширять.
7. Д-3, Д-вх, В-1: дуга наружу — по плану заказчика, не проверено; блок оставить или заменить — не решено.

1000 мм · печать 1:1

Изм.	Кол.уч	Лист	№ док.	Подп.	Дата
Разраб.		Кырлан А.С.			21.10.26
Пров.					
ГИП					
Н. контр.					
Утв.					

ГД-2026-010-АИ

Дом 331 м²

Общая площадь 270,67* м² · * размеры приняты, не замерены (реестр — л. 7, К-1)

Дизайн-проект интерьера

Стадия	Лист	Листов
РП	19	159

План дверей и ведомость заполнения проёмов · 1-й этаж

М 1:200

Кырлан Александр Сергеевич

выпуск 18.10.2026 № 9365d64cec · стр. 21 из 197

План дверей и ведомость заполнения проёмов · Мансарда

Проёмы, марки заполнения, привязки · размеры в мм

ПРЕДВАРИТЕЛЬНО · не для производства работ · открыто пунктов: 6 (реестр — л. 7)

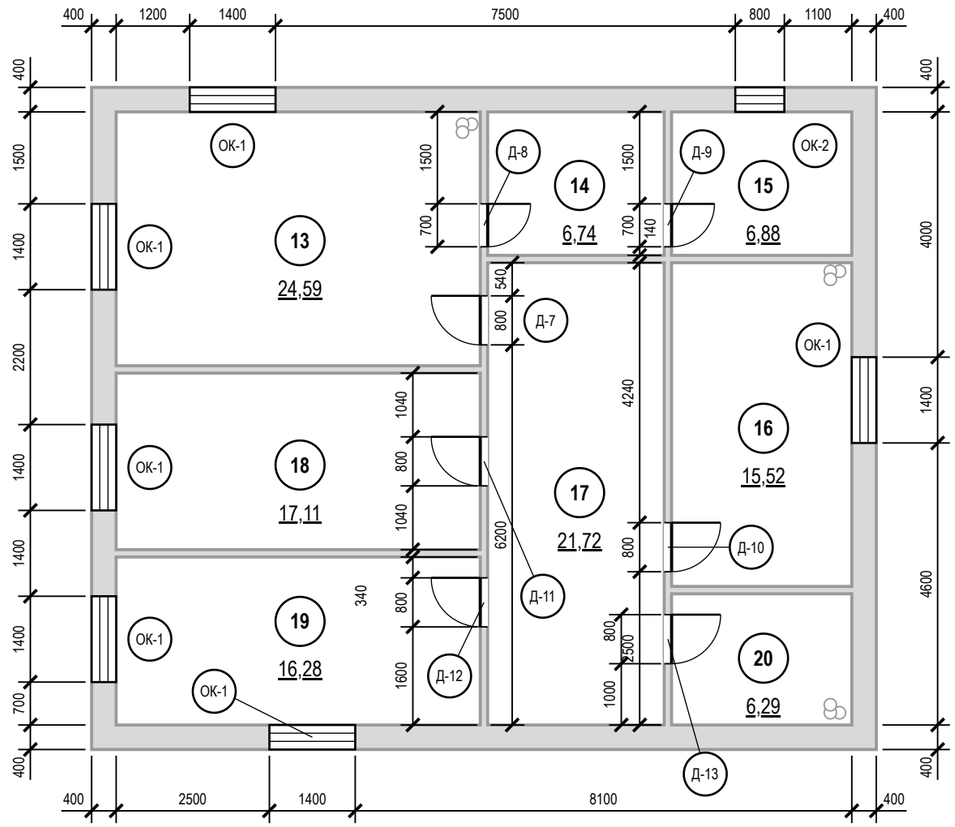

Ведомость заполнения проёмов

Марка	Наименование, обозначение	Проём ш×в, мм	Кол.	Откр.	Отделка полотна	Фурнитура	Прим.
Д-7	Дверь скрытого монтажа, ТУ изготовителя	800×2100	1	Л	окраска No. 226 с двух сторон	скрытые петли 3D, магнитный замок	
Д-8	Дверь скрытого монтажа, ТУ изготовителя	700×2100	1	П	No. 105 — пом. 14, No. 226 — пом. 13	скрытые петли 3D, магнитный замок	
Д-9	Дверь скрытого монтажа, ТУ изготовителя	700×2100	1	П	в тон облицовки — пом. 15, No. 105 — пом. 14	скрытые петли 3D, магнитный замок, фиксатор WC	порог 15
Д-10	Дверь скрытого монтажа, ТУ изготовителя	800×2100	1	П	окраска No. 226 с двух сторон	скрытые петли 3D, магнитный замок	
Д-11	Дверь скрытого монтажа, ТУ изготовителя	800×2100	1	Л	окраска No. 226 с двух сторон	скрытые петли 3D, магнитный замок	
Д-12	Дверь скрытого монтажа, ТУ изготовителя	800×2100	1	Л	окраска No. 226 с двух сторон	скрытые петли 3D, магнитный замок	
Д-13	Дверь скрытого монтажа, ТУ изготовителя	800×2100	1	П	в тон облицовки — пом. 20, No. 226 — пом. 17	скрытые петли 3D, магнитный замок, фиксатор WC	порог 15
ОК-1	Блок оконный, ГОСТ 23166-2021	1400×1500	6				низ 900
ОК-2	Блок оконный, ГОСТ 23166-2021	800×800	1				низ 1500

Условные обозначения

- стены (подложка обмера)
- дверь распашная, дуга открывания
- дверь скрытого монтажа
- оконный блок
- Д — марка типа (Д-N, ОК-N)
- 1 — номер помещения, площадь м²

Примечания

1. Размеры проёмов и привязки — в миллиметрах от чистых граней стен до отделки; привязка — от угла того помещения, со стороны которого стоит размер. Размер в ведомости — ширина × высота проёма от чистого пола 0,000. Откос от угла помещения до проёма с коробкой — не менее 50 мм.
2. Марки в кружках — типы заполнения проёмов (ГОСТ 21.501-2018, п. 5.3.2); одна марка — один типоразмер; количество сверено с планом.
3. Открывание: Л — петли слева, П — справа, если смотреть со стороны, куда открывается полотно (на себя).
4. Скрытые двери (Д-7…Д-13): проём замерить в чистоте; блок заказать до штукатурки (≈ 30 дн.), короб ставить до штукатурки; полотно навесить после чистовой отделки, красить в цвет стен. Порядок практика монтажа, изготовитель подтверждает.
5. Размер в ведомости — проёма: полотно скрытой двери уже проёма на коробку и зазор 10–15 мм (модель не выбрана); Д-7…Д-13 — существующие проёмы, до техзаключения не расширять.

Допущения и предложения на листе

Основа листа: размеры и контуры этажей подобраны проектировщиком по составу помещений и площадям этажей с картинки 470 px (размеры на ней не читаются); обмер и исходный проект — задание (К-1); высоты: 1-й этаж 2800 мм, мансарда 2700 мм (горизонтальная часть) приняты; скаты кровли мансарды приняты по картинке: колено 1200 мм, уклон 45°, конёк вдоль длинной стороны; проект КР — задание (К-2); наружные стены 400 мм, перегородки 120 мм приняты (К-1); разрешённая мощность 15 кВт принята по типовым ТУ для частного дома (К-4); подрайон климата не задан — принят не северный (жилые от 2,5 м) (К-7).
См. лист открытых вопросов (лист 7, записи К-1, К-2, К-4, К-7).

1000 мм · печать 1:1

Изм.	Кол.уч	Лист	№ док.	Подп.	Дата
Разраб.		Кырлан А.С.			21.10.26
Пров.					
ГИП					
Н. контр.					
Утв.					

ГД-2026-010-АИ

Дом 331 м²

Общая площадь 270,67* м² · * размеры приняты, не замерены (реестр — л. 7, К-1)

Дизайн-проект интерьера

Стадия	Лист	Листов
РП	20	159

План дверей и ведомость заполнения проёмов · Мансарда

М 1:100

Кырлан Александр Сергеевич

выпуск 18.10.2026 № 9365d64cec · стр. 22 из 197

Лестница Л-1*

План марша, разрез 1-1, узел крепления стойки ограждения, спецификация · отметки от ±0,000 (чистый пол этажа 1) · размеры в мм

ПРЕДВАРИТЕЛЬНО · не для производства работ · открыто пунктов: 6 (реестр — л. 7)

План марша Л-1* (М 1:50) · 6. Холл с лестницей

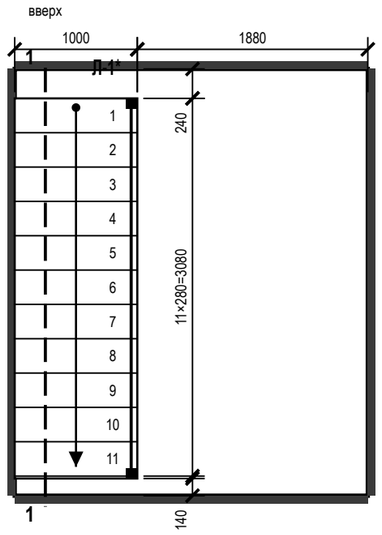

Разрез 1-1 (М 1:50)

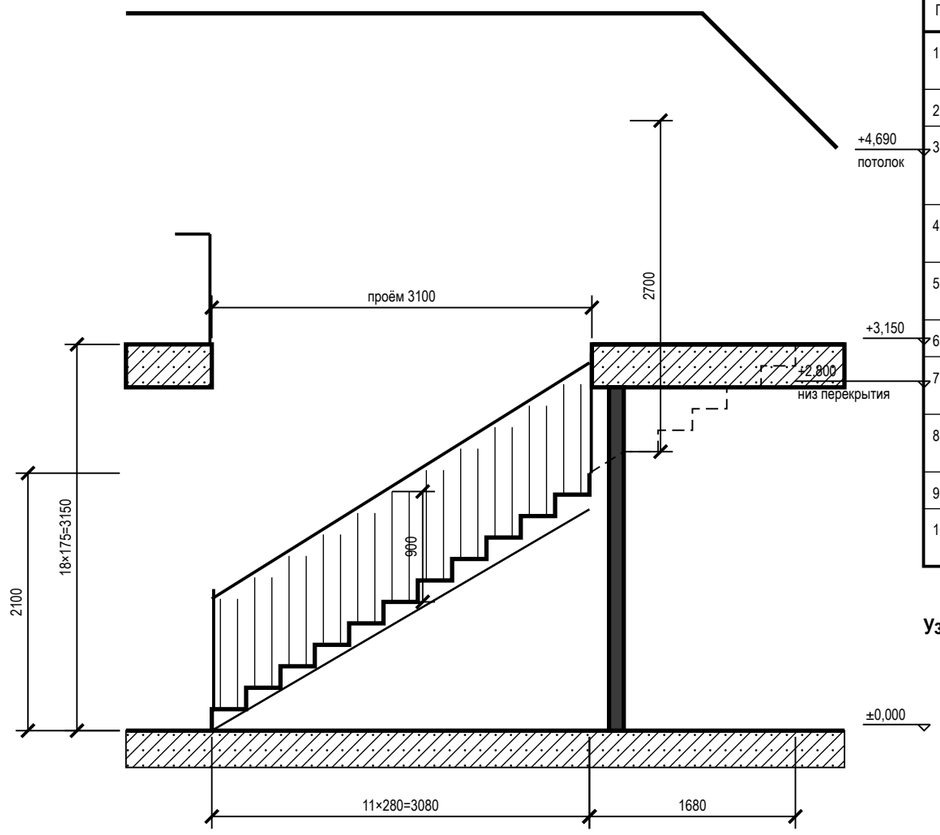

Спецификация элементов лестницы Л-1*

Поз.	Наименование	Кол.	Материал, сечение	Примечание
1	Ступень (проступь)	17	дуб, массив 40 мм, масло	1000×280, толщина по изделию
2	Подступенок	18	дуб 18 мм	высота 175
3	Косоур	2	косоуры стальные 80×40×4, порошковая окраска	несущие марша
4	Столб ограждения марша	2	сталь 20×20, порошковая окраска	по концам марша, стороны Б
5	Балясина	46	сталь 20×20, порошковая окраска	шаг 120, просвет 100
6	Поручень марша	1	дуб 40×60	L ≈ 5,61 м, h 900
7	Столб ограждения проёма	3	сталь 20×20, порошковая окраска	углы проёма, стороны А, Б
8	Балясина ограждения проёма	34	сталь 20×20, порошковая окраска	шаг 120
9	Поручень ограждения проёма	1	дуб 40×60	L ≈ 4,10 м, h 900
10	Крепёж ограждения	1	комплект по изделию	нагрузка на поручень 0,5 кН/м

Узел 1. Крепление стойки ограждения (М 1:5)

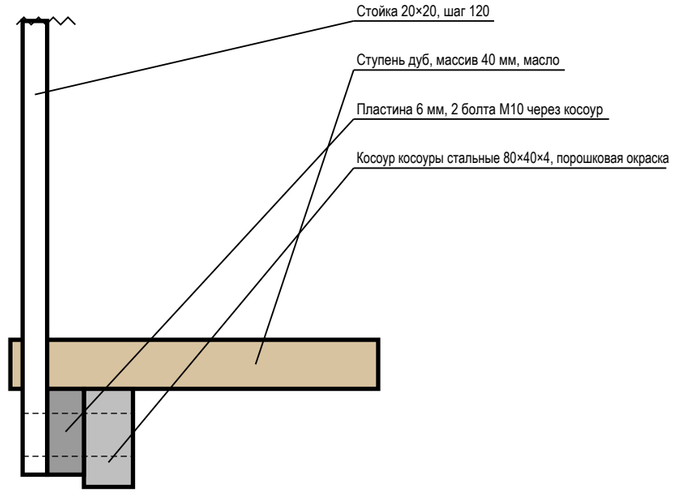

Зазор заполнения до ступени 100 (ГОСТ 25772, прил. А); узел типовой, уточнить по изделию

Примечания

1. Лестница Л-1*: 18 подъёмов × 175 мм = 3150 мм (отм. ±0,000 … +3,150), проступь 280 мм, ширина марша 1000 мм; уклон 32,0°, шаг 2h + b = 630 мм (удобно 600–640 — практика).
2. В габарит марша 3100 мм входят 11 проступей (до отм. +2,100); до пола этажа выше нужно 17 проступей — 4760 мм (показаны штрихом): одномаршевая лестница в этом помещении не встаёт, решение по реестру (К-6).
3. Ограждение марша со стороны Б: балясины, просвет между элементами 100 мм (не больше 150 — ГОСТ 25772-2025, табл. 3, тип МВ); высота 900 мм, поручень с одной стороны на 900 мм по линии носков (не менее 900 — СП 55.13330.2016, п. 8.3; СП 59.13330.2020, п. 6.2.11).
4. Проём в перекрытии 1000×3100 мм на этаже 2 ограждён со сторон А, Б высотой 900 мм, непрерывно, с поручнем (СП 55.13330.2016, п. 8.3); нагрузка на поручень 0,5 кН/м (СП 20.13330.2016, п. 8.2.6).
5. Просвет над линией носков — не менее 2700 мм (ступень 13, под потолком мансарды); рекомендуется не менее 2000, путь эвакуации — 2200 (СП 55.13330.2016, п. 7.4).
6. Все подступенки одной высоты (СП 55.13330.2016, п. 8.2). Размеры по месту уточнить после обмера: разность отметок чистых полов замерить до заказа изделия.
7. Узел 1 — типовое решение крепления стойки к косоуру; крепёж, сечения и материал — по проекту изделия изготовителя лестницы.

Допущения и предложения на листе

Основа листа: размеры и контуры этажей подобраны проектировщиком по составу помещений и площадям этажей с картинки 470 px (размеры на ней не читаются); обмер и исходный проект — задание (К-1); высоты: 1-й этаж 2800 мм, мансарда 2700 мм (горизонтальная часть) приняты; скаты кровли мансарды приняты по картинке: колено 1200 мм, уклон 45°, конёк вдоль длинной стороны; проект КР — задание (К-2); наружные стены 400 мм, перегородки 120 мм приняты (К-1); разрешённая мощность 15 кВт принята по типовым ТУ для частного дома (К-4); подрайон климата не задан — принят не северный (жилые от 2,5 м) (К-7).

Знак «*» — принято, не замерено и не подтверждено (замерить на объекте): К-6: Л-1 — габарит марша снят с картинки заказчика (11 проступей в холле 3,6 м), а до отм. +3,150 нужно 18 подъёмов — одномаршевая не встаёт: решение по К-6.

См. лист открытых вопросов (лист 7, записи К-1, К-2, К-4, К-6, К-7).

1000 мм · печать 1:1

Изм.	Кол.уч	Лист	№ док.	Подп.	Дата
Разраб.		Кырлан А.С.			21.10.26
Пров.					
ГИП					
Н. контр.					
Утв.					

ГД-2026-010-АИ

Дом 331 м²

Общая площадь 270,67* м² · * размеры приняты, не замерены (реестр — л. 7, К-1)

Дизайн-проект интерьера

Стадия	Лист	Листов
РП	21	159

Лестница Л-1

М 1:50

Кырлан Александр Сергеевич

выпуск 18.10.2026 № 9365d64cec · стр. 23 из 197

Концепция интерьера · 1-й этаж

Шале · схема комплементарная · 60/30/10 · материалы, образы и зонирование

ПРЕДВАРИТЕЛЬНО · не для производства работ · открыто пунктов: 6 (реестр — л. 7)

Идея

Стиль — шале: защищённый, тёплый, основательный, природный, камерный, после мороза — у огня. Современное шале 60 % + эко (eco-organic.json) 40 %: загородный дом у леса. Стены — шерстяной белый Joa's White No. 226 и молочный S 0804-Y30R, потолки — известковый Slaked Lime No. 105; второй план — выцветший оливковый V451, шалфей S 3020-G30Y, песчаник X463; акценты — хвойный S 7020-G10Y, терракота Red Earth No. 64, брусника Eating Room Red No. 43. Дерево — дуб и лиственница под маслом, камень у камина. Цветовая схема — комплементарная, пропорция 60/30/10: база на стенах и потолках, вторичный цвет — в текстиле и мягкой мебели, акцент — точечно.

Мудборд: материалы и фактуры

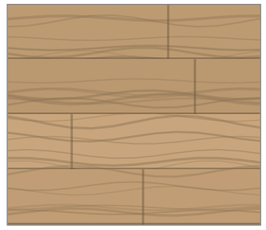

1167-4250
пол

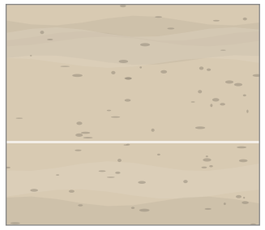

Керамогранит матовый
фартук

Slaked Lime · Little Greene No. 105
потолок, стены, плинтус

Joa's White · Farrow & Ball No. 226
стены, плинтус

NCS S 0804-Y30R
стены, потолок, плинтус

Bancha · Farrow & Ball No. 298
акцент (стена А)

Studio Green — почти чёрный зелёный · Farrow & Ball No. 93
акцент (стена А)

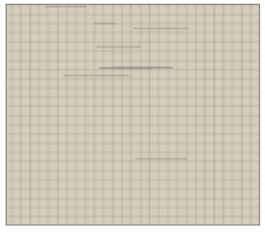

Лён, NCS S 2005-Y20R
Рулонная штора кассетная, Портьеры-волна

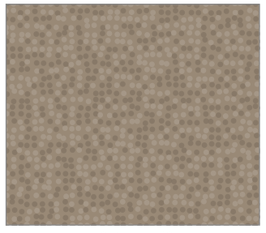

Шерсть, Farrow & Ball No. 40
портьеры на люверсах

Палитра 60/30/10

60 % база — Farrow & Ball No. 226 Joa's White, LRV 63; NCS S 0804-Y30R, LRV 85; Little Greene No. 105 Slaked Lime, LRV 82

30 % вторичный — Tikkurila V451, LRV 51; NCS S 3020-G30Y, LRV 38; Tikkurila X463, LRV 51; Farrow & Ball No. 229 Elephant's Breath — тёплый средне-серый с лиловым подтоном, LRV 52; Farrow & Ball No.

10 % акцент — NCS S 7020-G10Y Хвойный тёмно-зелёный, LRV 5; Farrow & Ball No. 64 Red Earth, LRV 18; Farrow & Ball No. 43 Eating Room Red — брусничный красный, LRV 11.8

Функциональное зонирование (М 1:200)

дневная зона: гостиная, кухня, столовая
мокрая зона: санузлы
хранение: гардеробная, кладовая
вход и коммуникации
(1) номер помещения (лист 24)

Образы помещений

5. Гостиная 33,74 м²
стены NCS S 0804-Y30R; акцент No. 93 на стене

1. Кухня-столовая 24,59 м²
стены NCS S 0804-Y30R

2. Кабинет-гостевая 11,92 м²
стены Farrow & Ball No. 226; акцент No. 298 на

8. Прихожая 12,46 м²
стены Farrow & Ball No. 226

9. Тамбур 3,49 м²
стены Farrow & Ball No. 226

6. Холл с лестницей 10,02 м²
стены Farrow & Ball No. 226

3. Санузел 1 этажа 4,87 м²
стены Atlas Concorde A8UZ

4. Котельная 6,88 м²
стены Farrow & Ball No. 226

7. Кладовая 5,99 м²
стены Little Greene No. 105

10. Гараж 41,58 м²
стены Farrow & Ball No. 226

11. Веранда 21,84 м²
стены NCS S 0804-Y30R

12. Крыльцо 3,38 м²
стены NCS S 0804-Y30R

Материалы и отделка

1167-4250
пол — пом. 1, 2, 5, 6, 7

Керамогранит матовый
тон F497; 600×600
фартук — пом. 1

A8UZ
пол, стены — пом. 3, 4, 8, 9, 11, 12

Плинтус из керамогранита пола
подрезка 80 мм, верхняя кромка с запилом 45°
плинтус — пом. 11, 12

NCS S 0804-Y30R, LRV 85
Tikkurila Luja 7
стены, потолок, плинтус — пом. 1, 5, 11, 12

Farrow & Ball No. 226 Joa's White, LRV 63
Farrow & Ball Modern Emulsion, матовая
стены, плинтус — пом. 2, 4, 6, 8, 9, 10

Little Greene No. 105 Slaked Lime, LRV 82
Tikkurila Anti-Reflex 2, глубокоматовая
потолок, стены, плинтус — пом. 2, 3, 4, 6, 7, 8, 9, 10

Farrow & Ball No. 298 Bancha, LRV 14
акцентная стена
акцент (стена А) — пом. 2

Farrow & Ball No. 93 Studio Green — почти чёрный зелёный, LRV 7
акцентная стена
акцент (стена А) — пом. 5

Текстиль и металл

Лён, NCS S 2005-Y20R
Рулонная штора кассетная, Портьеры-волна

Шерсть, Farrow & Ball No. 40
портьеры на люверсах

Вуаль, NCS S 0804-Y30R
тюль, Тюль-вуаль

Шерсть, Tikkurila X463
ковёр джутовый под диваном

Лён, NCS S 3010-Y30R
подушки на диван

Бархат, Farrow & Ball No. 298
подушки на кровать

Шерсть, Farrow & Ball No. 298
плед на кровать

Шерсть, Farrow & Ball No. 243
ковёр мягкой группы

Лён, Farrow & Ball No. 226
подушки декоративные на диван

Бархат, Farrow & Ball No. 93
Подушки декоративные на диван

Чего избегаем

1) Эффект сауны: сосна под оранжевым лаком на стенах, потолке и полу одновременно
2) Тёмное дерево в низкой комнате без светлого потолка
3) Пластиковые/полиуретановые балки с повторяющимся рисунком
4) Избыток трофеев, рогов и шкур — охотничий домик
5) Заставленность альпийскими сувенирами
6) Холодный свет и много точек в потолке

Допущения и предложения на листе

Основа листа: размеры и контуры этажей подобраны проектировщиком по составу помещений и площадям этажей с картинки 470 px (размеры на ней не читаются); обмер и исходный проект — задание (К-1); высоты: 1-й этаж 2800 мм, мансарда 2700 мм (горизонтальная часть) приняты; скаты кровли мансарды приняты по картинке: колено 1200 мм, уклон 45°, конёк вдоль длинной стороны; проект КР — задание (К-2); наружные стены 400 мм, перегородки 120 мм приняты (К-1); разрешённая мощность 15 кВт принята по типовым ТУ для частного дома (К-4); подрайон климата не задан — принят не северный (жилые от 2,5 м) (К-7).
См. лист открытых вопросов (лист 7, записи К-1, К-2, К-4, К-7).

Примечания

1. Коды цвета — по веерам производителей (колерная карта, лист 73); перед закупкой краски — выкрас на стене объекта под дневным светом и лампами проекта.
2. Материалы — по ведомости отделки (лист 70); мебель, текстиль и декор — по спецификации (лист 26). Образцы доски, керамогранита и тканей утвердить до заказа.
3. Фактуры на листе условные, цвет передан по HEX-значениям производителей: при печати возможны отклонения, решение — только по физическому образцу.

Изм.	Кол.уч	Лист	№ док.	Подп.	Дата
Разраб.		Кырлан А.С.			21.10.26
Пров.					
ГИП					
Н. контр.					
Утв.					

ГД-2026-010-АИ

Дом 331 м²

Общая площадь 270,67* м² · * размеры приняты, не замерены (реестр — л. 7, К-1)

Дизайн-проект интерьера

Стадия	Лист	Листов
РП	22	159

Концепция интерьера · 1-й этаж

М б/м

Кырлан Александр Сергеевич

выпуск 18.10.2026 № 9365d64cec · стр. 24 из 197

Концепция интерьера · Мансарда

Шале · схема комплементарная · 60/30/10 · материалы, образы и зонирование

ПРЕДВАРИТЕЛЬНО · не для производства работ · открыто пунктов: 6 (реестр — л. 7)

Идея

Стиль — шале: защищённый, тёплый, основательный, природный, камерный, после мороза — у огня. Современное шале 60 % + эко (eco-organic.json) 40 %: загородный дом у леса. Стены — шерстяной белый Joa's White No. 226 и молочный S 0804-Y30R, потолки — известковый Slaked Lime No. 105; второй план — выцветший оливковый V451, шалфей S 3020-G30Y, песчаник X463; акценты — хвойный S 7020-G10Y, терракота Red Earth No. 64, брусника Eating Room Red No. 43. Дерево — дуб и лиственница под маслом, камень у камина. Цветовая схема — комплементарная, пропорция 60/30/10: база на стенах и потолках, вторичный цвет — в текстиле и мягкой мебели, акцент — точечно.

Мудборд: материалы и фактуры

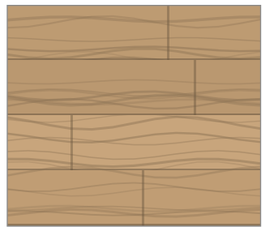

1167-4250
пол

A8UZ
пол, стены

Slaked Lime · Little Greene No. 105
потолок, стены, плинтус

Joa's White · Farrow & Ball No. 226
стены, плинтус

Хвойный тёмно-зелёный · NCS S 7020-G10Y
акцент (стена А)

Red Earth · Farrow & Ball No. 64
акцент (стена А)

NCS S 3020-G30Y
акцент (стена А)

NCS S 3040-Y70R
акцент (стена А)

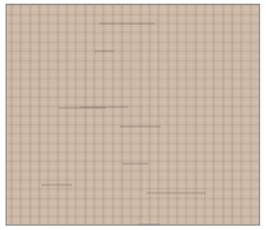

Лён, Tikkurila X463
портьеры-волна, подушки декоративные на кровать

Палитра 60/30/10

60 % база — Farrow & Ball No. 226 Joa's White, LRV 63; NCS S 0804-Y30R, LRV 85; Little Greene No. 105 Slaked Lime, LRV 82

30 % вторичный — Tikkurila V451, LRV 51; NCS S 3020-G30Y, LRV 38; Tikkurila X463, LRV 51; Farrow & Ball No. 229 Elephant's Breath — тёплый средне-серый с лиловым подтоном, LRV 52; Farrow & Ball No.

10 % акцент — NCS S 7020-G10Y Хвойный тёмно-зелёный, LRV 5; Farrow & Ball No. 64 Red Earth, LRV 18; Farrow & Ball No. 43 Eating Room Red — брусничный красный, LRV 11.8

Функциональное зонирование (М 1:200)

ночная зона: спальни
мокрая зона: санузлы
хранение: гардеробная, кладовая
вход и коммуникации
(1) номер помещения (лист 24)

Образы помещений

13. Спальня мастер — 24,59 м²

стены Farrow & Ball No. 226; акцент S 7020-G10Y на стене А
пол — 1167-4250
текстиль: портьеры No. 229, тюль No. 105, ковёр S 2005-Y20R

16. Спальня 2 — 15,52 м²

стены Farrow & Ball No. 226; акцент No. 64 на стене А
пол — 1167-4250
текстиль: портьеры X463, тюль No. 105, ковёр S 3010-Y30R

18. Спальня 3 — 17,11 м²

стены Farrow & Ball No. 226; акцент S 3020-G30Y на стене А
пол — 1167-4250
текстиль: портьеры на люверсах V451, тюль S 0804-Y30R, ковёр S 2005-Y20R

19. Спальня 4 — 16,28 м²

стены Farrow & Ball No. 226; акцент S 3040-Y70R на стене А
пол — 1167-4250
текстиль: портьеры S 2005-Y20R, тюль No. 226, ковёр S 3010-Y30R

17. Холл мансарды — 21,72 м²

стены Farrow & Ball No. 226
пол — 1167-4250
текстиль: коврик для йоги и растяжки 1830×610×6 S 3020-G30Y
декор: Монстера в кашпо

14. Гардеробная мастер — 6,74 м²

стены Little Greene No. 105
пол — 1167-4250
свет 3000 K

15. Санузел мастер — 6,88 м²

стены Atlas Concorde A8UZ
пол — A8UZ
свет 3000 K

20. Санузел 2 — 6,29 м²

стены Atlas Concorde A8UZ
пол — A8UZ
свет 3000 K

Материалы и отделка

1167-4250
пол — пом. 13, 14, 16, 17, 18, 19

A8UZ
пол, стены — пом. 15, 20

Farrow & Ball No. 226 Joa's White, LRV 63
Farrow & Ball Modern Emulsion, матовая
стены, плинтус — пом. 13, 16, 17, 18, 19

Little Greene No. 105 Slaked Lime, LRV 82
Tikkurila Anti-Reflex 2, глубокоматовая
потолок, стены, плинтус — пом. 13, 14, 15, 16, 17, 18, 19, 20

NCS S 7020-G10Y Хвойный тёмно-зелёный, LRV 5
акцентная стена
акцент (стена А) — пом. 13

Farrow & Ball No. 64 Red Earth, LRV 18
акцентная стена
акцент (стена А) — пом. 16

NCS S 3020-G30Y, LRV 38
акцентная стена
акцент (стена А) — пом. 18

NCS S 3040-Y70R, LRV 24
акцентная стена
акцент (стена А) — пом. 19

Текстиль и металл

Шерсть, Farrow & Ball No. 229
портьеры-волна

Вуаль, Little Greene No. 105
тюль

Шерсть, NCS S 2005-Y20R
ковёр под кроватью, подушки декоративные на кровать

Бархат, NCS S 7020-G10Y
подушки на кровать

Шерсть, NCS S 7020-G10Y
плед на кровать

Лён, Tikkurila X463
портьеры-волна, подушки декоративные на кровать

Шерсть, NCS S 3010-Y30R
ковёр под кроватью

Бархат, Farrow & Ball No. 64
подушки на кровать

Шерсть, Farrow & Ball No. 64
плед на кровать

Чёрный матовый металл
зеркало в рост, зеркало безопасное

Чего избегаем

1) Эффект сауны: сосна под оранжевым лаком на стенах, потолке и полу одновременно
2) Тёмное дерево в низкой комнате без светлого потолка
3) Пластиковые/полиуретановые балки с повторяющимся рисунком
4) Избыток трофеев, рогов и шкур — охотничий домик
5) Заставленность альпийскими сувенирами
6) Холодный свет и много точек в потолке

Допущения и предложения на листе

Основа листа: размеры и контуры этажей подобраны проектировщиком по составу помещений и площадям этажей с картинки 470 px (размеры на ней не читаются); обмер и исходный проект — задание (К-1); высоты: 1-й этаж 2800 мм, мансарда 2700 мм (горизонтальная часть) приняты; скаты кровли мансарды приняты по картинке: колено 1200 мм, уклон 45°, конёк вдоль длинной стороны; проект КР — задание (К-2); наружные стены 400 мм, перегородки 120 мм приняты (К-1); разрешённая мощность 15 кВт принята по типовым ТУ для частного дома (К-4); подрайон климата не задан — принят не северный (жилые от 2,5 м) (К-7).
См. лист открытых вопросов (лист 7, записи К-1, К-2, К-4, К-7).

Примечания

1. Коды цвета — по веерам производителей (колерная карта, лист 73); перед закупкой краски — выкрас на стене объекта под дневным светом и лампами проекта.
2. Материалы — по ведомости отделки (лист 70); мебель, текстиль и декор — по спецификации (лист 26). Образцы доски, керамогранита и тканей утвердить до заказа.
3. Фактуры на листе условные, цвет передан по HEX-значениям производителей: при печати возможны отклонения, решение — только по физическому образцу.

Изм.	Кол.уч	Лист	№ док.	Подп.	Дата
Разраб.		Кырлан А.С.			21.10.26
Пров.					
ГИП					
Н. контр.					
Утв.					

ГД-2026-010-АИ

Дом 331 м²

Общая площадь 270,67* м² · * размеры приняты, не замерены (реестр — л. 7, К-1)

Дизайн-проект интерьера

Стадия	Лист	Листов
РП	23	159

Концепция интерьера · Мансарда

М б/м

Кырлан Александр Сергеевич

План расстановки мебели · 1-й этаж

Мебель и оборудование · размеры в мм от чистовых стен · марки — по ведомости

ПРЕДВАРИТЕЛЬНО · не для производства работ · открыто пунктов: 6 (реестр — л. 7)

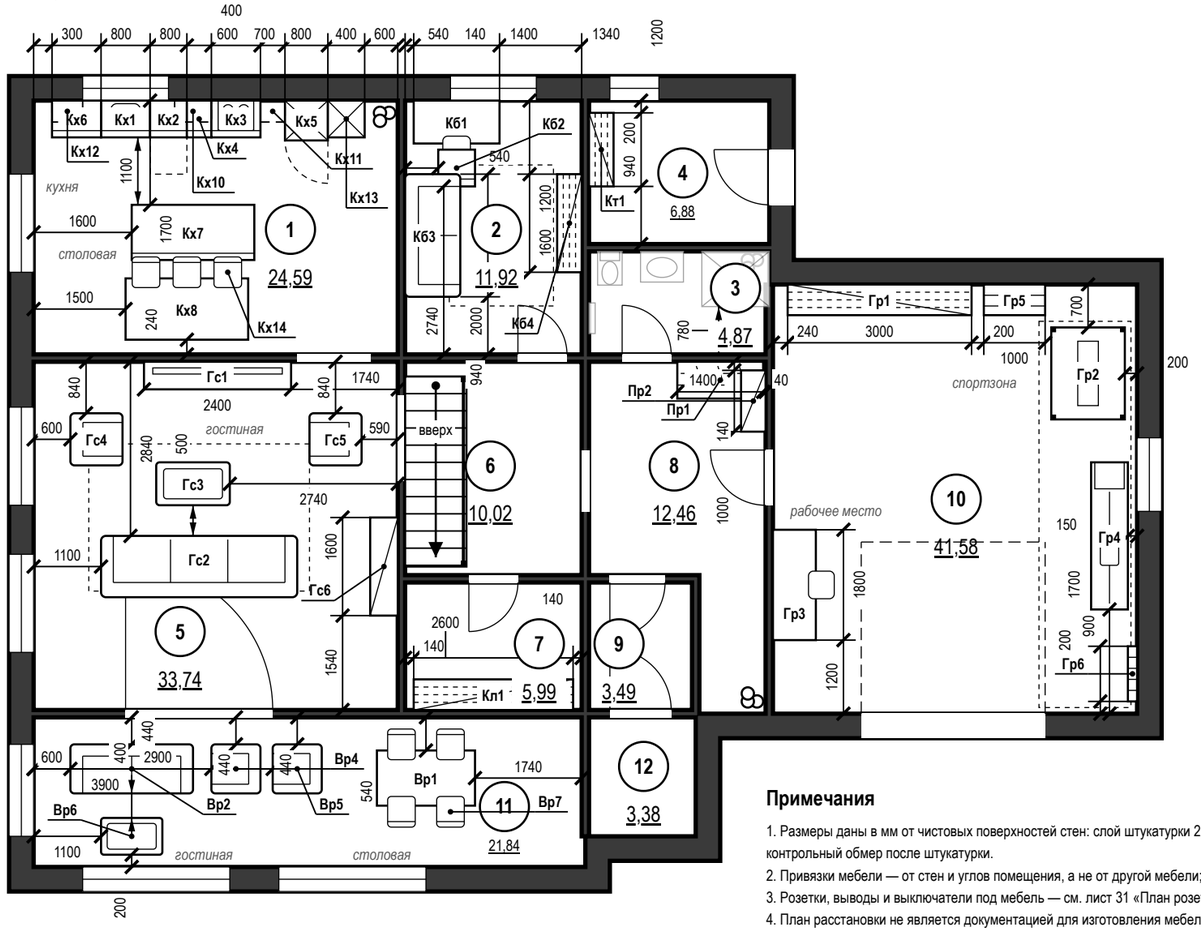

Экспликация помещений

лист 15 · на плане — номера в марках

Ведомость мебели и оборудования

39 позиц. (44 шт.) — не помещается на листе:
полностью на листе 26 «Спецификация мебели и оборудования»
марка, наименование, Ш×Г×В, материал, модель,
допуск замены. Марки на плане — по ней.

Условные обозначения

- мебель и оборудование — габарит в масштабе
- навесные шкафы (низ выше 0,9 м) — невидимый контур
- ковёр
- зона открывания дверец шкафов и техники
- К1 — марка предмета по ведомости мебели
- привязка от чистовой стены, мм
- ширина прохода, зазор, мм
- сантехприборы — подложка (лист ВК)
- существующие стены (сечение)
- стояк: К1 — канализация, В1 — ХВС, Т3 — ГВС
- 1 — номер помещения, площадь м²
- *зона* — функциональная зона помещения

Примечания

1. Размеры даны в мм от чистовых поверхностей стен: слой штукатурки 20 мм по блоку и 5 мм шпаклёвки по ГКЛ учтён. Перед заказом встроенной мебели контрольный обмер после штукатурки.
2. Привязки мебели — от стен и углов помещения, а не от другой мебели; ширина проходов и зазоров показана стрелками.
3. Розетки, выводы и выключатели под мебель — см. лист 31 «План розеток и электровыводов · 1-й этаж»; сантехприборы и выводы воды — лист 49.
4. План расстановки не является документацией для изготовления мебели: изделия — по чертежам мебельщика; покупную мебель заменять только на изделия не больше габарита из спецификации (лист 26).
5. Встроенная мебель «стена в стену» — с зазором 10 мм с каждой стороны или с компенсаторами.
6. Стулья обеденной группы (Кх14 — 3 шт., Вр7 — 4 шт.) показаны в рабочем положении, задвинутыми под столешницу на 150 мм.

Допущения и предложения на листе

Основа листа: размеры и контуры этажей подобраны проектировщиком по составу помещений и площадям этажей с картинки 470 px (размеры на ней не читаются); обмер и исходный проект — задание (К-1); высоты: 1-й этаж 2800 мм, мансарда 2700 мм (горизонтальная часть) приняты; скаты кровли мансарды приняты по картинке: колено 1200 мм, уклон 45°, конёк вдоль длинной стороны; проект КР — задание (К-2); наружные стены 400 мм, перегородки 120 мм приняты (К-1); разрешённая мощность 15 кВт принята по типовым ТУ для частного дома (К-4); подрайон климата не задан — принят не северный (жилые от 2,5 м) (К-7).
Открытые вопросы и конфликты по листу: К-1.
См. лист открытых вопросов (лист 7, записи К-1, К-2, К-4, К-7).

1000 мм · печать 1:1

Изм.	Кол.уч	Лист	№ док.	Подп.	Дата
Разраб.		Кырлан А.С.			21.10.26
Пров.					
ГИП					
Н. контр.					
Утв.					

ГД-2026-010-АИ

Дом 331 м²

Общая площадь 270,67* м² · * размеры приняты, не замерены (реестр — л. 7, К-1)

Дизайн-проект интерьера

Стадия	Лист	Листов
РП	24	159

План расстановки мебели · 1-й этаж

М 1:100

Кырлан Александр Сергеевич

выпуск 18.10.2026 № 9365d64cec · стр. 26 из 197

План расстановки мебели · Мансарда

Мебель и оборудование · размеры в мм от чистовых стен · марки — по ведомости

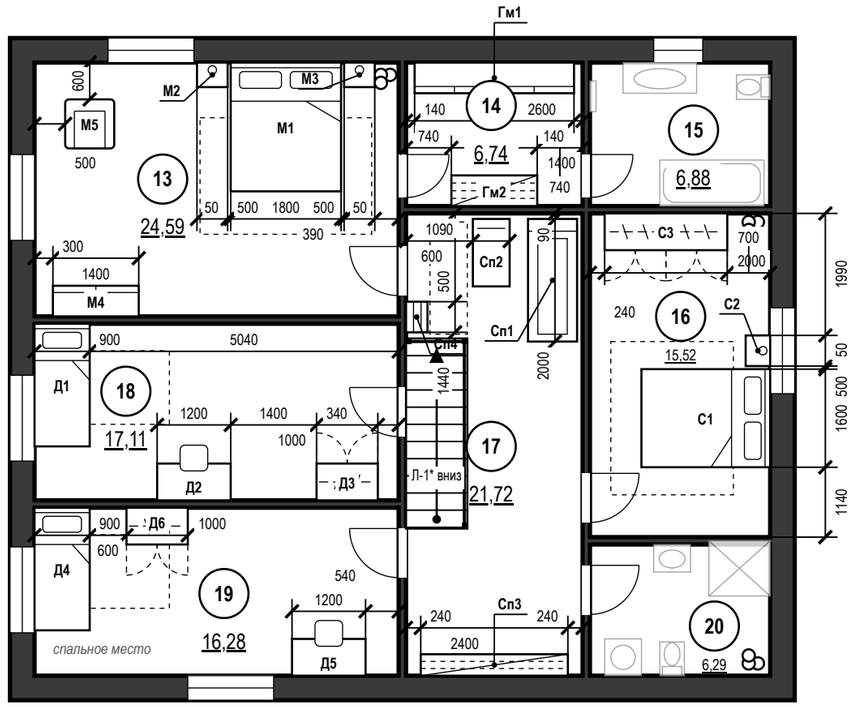

Примечания

1. Размеры даны в мм от чистовых поверхностей стен: слой штукатурки 20 мм по блоку и 5 мм шпаклёвки по ГКЛ учтён. Перед заказом встроенной мебели контрольный обмер после штукатурки.
2. Привязки мебели — от стен и углов помещения, а не от другой мебели.
3. Розетки, выводы и выключатели под мебель — см. лист 31 «План розеток и электровыводов · 1-й этаж»; сантехприборы и выводы воды — лист 49.
4. План расстановки не является документацией для изготовления мебели: изделия — по чертежам мебельщика; покупную мебель заменять только на изделия не больше габарита из спецификации (лист 26).
5. Встроенная мебель «стена в стену» — с зазором 10 мм с каждой стороны или с компенсаторами.
6. Отступ от стены, на плане не образмерен: Сп1 — 90 мм, Сп2 — 90 мм.

Допущения и предложения на листе

Основа листа: размеры и контуры этажей подобраны проектировщиком по составу помещений и площадям этажей с картинки 470 px (размеры на ней не читаются); обмер и исходный проект — задание (К-1); высоты: 1-й этаж 2800 мм, мансарда 2700 мм (горизонтальная часть) приняты; скаты кровли мансарды приняты по картинке: колено 1200 мм, уклон 45°, конёк вдоль длинной стороны; проект КР — задание (К-2); наружные стены 400 мм, перегородки 120 мм приняты (К-1); разрешённая мощность 15 кВт принята по типовым ТУ для частного дома (К-4); подрайон климата не задан — принят не северный (жилые от 2,5 м) (К-7).
Знак «*» — принято, не замерено и не подтверждено (замерить на объекте): К-6: Л-1 — габарит марша снят с картинки заказчика (11 проступей в холле 3,6 м), а до отм. +3,150 нужно 18 подъёмов — одномаршевая не встаёт: решение по К-6.
Открытые вопросы и конфликты по листу: К-1.
См. лист открытых вопросов (лист 7, записи К-1, К-2, К-4, К-6, К-7).

1000 мм · печать 1:1

Экспликация помещений

лист 15 · на плане — номера в марках

Ведомость мебели и оборудования

Марка	Наименование	Ш×Г×В, мм	Пом.	Кол.
М1	Кровать 1800×2000	1800×2100×450	13	1
М2	Тумба прикроватная	500×400×550	13	1
М3	Тумба прикроватная	500×400×550	13	1
М4	Комод	1400×500×800	13	1
М5	Кресло для чтения	800×800×900	13	1
Гм1	Ящики низкие под скатом	2600×500×1100	14	1
Гм2	Система хранения открытая в	1400×500×2400	14	1
С1	Кровать 1600×2000	1600×2100×450	16	1
С2	Тумба подвесная	500×400×550	16	1
С3	Шкаф распашной	2000×600×2400	16	1
Сп1	Дорожка беговая складная	2000×800×1400	17	1
Сп2	Велотренажёр магнитный	600×1100×1150	17	1
Сп3	Стеллаж низкий под скатом	2400×350×900	17	1
Сп4	Стойка-этажерка для инвентаря	500×350×1000	17	1
Д1	Кровать 900×2000 с бортиком	900×2000×450	18	1
Д2	Стол письменный	1200×600×750	18	1
Д3	Шкаф распашной	1000×600×2200	18	1
Д4	Кровать 900×2000 с ящиками	900×2000×450	19	1
Д5	Стол письменный растущий	1200×600×750	19	1
Д6	Шкаф распашной	1000×600×2200	19	1

Ш — вдоль стены (изголовья), Г — от стены (длина кровати)
Материалы, модели, допуск замены — лист 26

Условные обозначения

- мебель и оборудование — габарит в масштабе
- ковёр
- зона открывания дверец шкафов и техники
- **К1** — марка предмета по ведомости мебели
- привязка от чистовой стены, мм
- сантехприборы — подложка (лист ВК)
- существующие стены (сечение)
- стояк: К1 — канализация, В1 — ХВС, Т3 — ГВС
- (1) — номер помещения, площадь м²
- *зона* — функциональная зона помещения

Изм.	Кол.уч	Лист	№ док.	Подп.	Дата
Разраб.		Кырлан А.С.			21.10.26
Пров.					
ГИП					
Н. контр.					
Утв.					

ГД-2026-010-АИ

Дом 331 м²

Общая площадь 270,67* м² · * размеры приняты, не замерены (реестр — л. 7, К-1)

Дизайн-проект интерьера

Стадия	Лист	Листов
РП	25	159

План расстановки мебели · Мансарда

М 1:100

Кырлан Александр Сергеевич

выпуск 18.10.2026 № 9365d64cec · стр. 27 из 197

01

Планировочное решение

Кырлан Александр Сергеевич

выпуск 18.10.2026 № 9365d64cec · стр. 28 из 197

Спецификация мебели и оборудования

ПРЕДВАРИТЕЛЬНО · не для производства работ · открыто пунктов: 6 (реестр — л. 7)

Форма 1 ГОСТ 21.110-2013 · позиции мебели — по плану расстановки

Поз.	Наименование и техническая характеристика	Тип, марка, обозначение документа, опросного листа	Код продукции	Поставщик	Ед. измерения	Кол.	Масса 1 ед., кг	Примечание
	Мебель встроенная и корпусная (изготовление по чертежам мебельщика)							
Кх1	Модуль под мойку у окна; корпус ЛДСП, фасады — матовая эмаль в тон стен; Ш×Г×В 800×600×900 мм			изготовление на заказ	шт.	1		пом. 1
Кх2	Посудомоечная машина встроенная; корпус ЛДСП, фасады — матовая эмаль в тон стен; Ш×Г×В 600×600×900 мм			изготовление на заказ	шт.	1		пом. 1
Кх3	Модуль с варочной панелью и духовым шкафом; корпус ЛДСП, фасады — матовая эмаль в тон стен; Ш×Г×В 800×600×900 мм			изготовление на заказ	шт.	1		пом. 1
Кх4	Модуль с ящиками; корпус ЛДСП, фасады — матовая эмаль в тон стен; Ш×Г×В 400×600×900 мм			изготовление на заказ	шт.	1		пом. 1
Кх5	Колонна с холодильником; корпус ЛДСП, фасады — матовая эмаль в тон стен; Ш×Г×В 700×650×2200 мм			изготовление на заказ	шт.	1		пом. 1
Кх6	Модуль с ящиками; корпус ЛДСП, фасады — матовая эмаль в тон стен; Ш×Г×В 800×600×900 мм			изготовление на заказ	шт.	1		пом. 1
Кх7	Остров с барной консолью из массива дуба, столешница — кварц; корпус ЛДСП, фасады — рейка из массива дуба, столешница — кварцевый агломерат 20 мм, консоль для завтрака — массив дуба 40 мм; Ш×Г×В 2000×900×900 мм			изготовление на заказ	шт.	1		пом. 1
Кх10	Навесной шкаф, фасад в тон острова; корпус ЛДСП, фасады — матовая эмаль в тон стен; Ш×Г×В 600×350×900 мм			изготовление на заказ	шт.	1		пом. 1
Кх11	Навесной шкаф узкий, полки для специй; корпус ЛДСП, фасады — матовая эмаль в тон стен; Ш×Г×В 400×350×900 мм			изготовление на заказ	шт.	1		пом. 1
Кх12	Полки открытые из массива дуба у окна, 3 яруса; полки — массив дуба 30 мм, масло; кронштейны — чёрная сталь; Ш×Г×В 500×350×900 мм			изготовление на заказ	шт.	1		пом. 1
Кх13	Пенал-кладовая с выдвижными корзинами; корпус ЛДСП, фасады — матовая эмаль в тон стен; Ш×Г×В 600×600×2200 мм			изготовление на заказ	шт.	1		пом. 1
Пр1	Шкаф-купе, светлый дуб; корпус ЛДСП, фасады — матовая эмаль в цвет стен (Farrow & Ball No. 226); Ш×Г×В 1400×600×2600 мм			изготовление на заказ	шт.	1		пом. 8
С3	Шкаф распашной, фасады — шпон ясеня с вертикальной рейкой; корпус ЛДСП, фасады — шпон ясеня с вертикальной рейкой, масло; Ш×Г×В 2000×600×2400 мм			изготовление на заказ	шт.	1		пом. 16
Д3	Шкаф распашной, фасады — матовая эмаль шалфей; корпус ЛДСП, фасады МДФ — матовая эмаль NCS S 3020-G30Y; Ш×Г×В 1000×600×2200 мм			изготовление на заказ	шт.	1		пом. 18
Д6	Шкаф распашной (вне ската), фасады — дуб и эмаль терракота; корпус ЛДСП, фасады — шпон дуба и МДФ в матовой эмали NCS S 3040-Y70R; Ш×Г×В 1000×600×2200 мм			изготовление на заказ	шт.	1		пом. 19
	Мебель покупная							
Кх8	Стол обеденный 2000×1000, массив дуба; шпон, дуб натуральный, матовое масло; Ш×Г×В 2000×1000×750 мм			аналог по характеристикам	шт.	1		пом. 1; замена ≤ габарита
Кх14	Стул обеденный к столу Кх8; обивка — ткань, цвет Tikkurila V451; каркас — дуб натуральный; Ш×Г×В 450×500×820 мм			аналог по характеристикам	шт.	3		пом. 1; замена ≤ габарита
Кб1	Письменный стол у окна, массив дуба на чёрном стальном подстолье; дерево — дуб массив, масло, металл — чёрный матовый; Ш×Г×В 1400×700×750 мм			аналог по характеристикам	шт.	1		пом. 2; замена ≤ габарита
Кб2	Кресло рабочее на колёсах, кожа коньячная; обивка кожа натуральная, коньяк; Ш×Г×В 600×600×900 мм			аналог по характеристикам	шт.	1		пом. 2; замена ≤ габарита
Кб3	Диван-кровать гостевой, шерстяной твид; обивка шерстяной твид, серо-оливковый меланж; Ш×Г×В 2000×900×850 мм			аналог по характеристикам	шт.	1		пом. 2; замена ≤ габарита
Кб4	Стеллаж для книг, чёрная сталь и полки из дуба; каркас — чёрная сталь, полки — массив дуба; Ш×Г×В 1600×400×2200 мм			аналог по характеристикам	шт.	1		пом. 2; крепление к стене; замена ≤ габарита
Кт1	Стеллаж технический; каркас и полки — ЛДСП, декор «дуб натуральный»; Ш×Г×В 1200×400×2000 мм			аналог по характеристикам	шт.	1		пом. 4; замена ≤ габарита
Гс1	ТВ-стена с камином, облицовка — колотый сланец; короб ГКЛ с облицовкой колотым сланцем, полка из массива дуба; Ш×Г×В 2400×450×600 мм			аналог по характеристикам	шт.	1		пом. 5; замена ≤ габарита
Гс2	Диван угловой, лён-рогожка; обивка лён-рогожка плотный, молочный; Ш×Г×В 3200×1000×820 мм			аналог по характеристикам	шт.	1		пом. 5; замена ≤ габарита
Гс3	Столик журнальный, столешница — сланец, подстолье дуб; столешница — сланец 20 мм, подстолье — массив дуба; Ш×Г×В 1200×700×420 мм			аналог по характеристикам	шт.	1		пом. 5; замена ≤ габарита

Примечания

1. Позиции мебели совпадают с марками на плане расстановки (лист 24); размеры Ш×Г×В — Ш вдоль стены, Г от стены.
2. Встроенная и корпусная мебель изготавливается по чертежам мебельщика после контрольного обмера; графы «Тип, марка» и «Код продукции» для неё не заполняются (ГОСТ 21.110-2013).
3. Покупные изделия — аналог по характеристикам: заменять только на изделия не больше указанного габарита и того же материала и цвета.
4. Материал и цвет, не указанные в данных изделия, приняты по концепции (лист 22): тон дерева — по полу, обивка — по вторичному цвету палитры; образцы согласовать до заказа.
5. Масса 1 ед. для изделий до 25 кг не указывается. Техника — по монтажным схемам изготовителя; выводы — по листам ЭОМ и ВК.

Допущения и предложения на листе

Основа листа: размеры и контуры этажей подобраны проектировщиком по составу помещений и площадям этажей с картинки 470 px (размеры на ней не читаются); обмер и исходный проект — задание (К-1); высоты: 1-й этаж 2800 мм, мансарда 2700 мм (горизонтальная часть) приняты; скаты кровли мансарды приняты по картинке: колено 1200 мм, уклон 45°, конёк вдоль длинной стороны; проект КР — задание (К-2); наружные стены 400 мм, перегородки 120 мм приняты (К-1); разрешённая мощность 15 кВт принята по типовым ТУ для частного дома (К-4); подрайон климата не задан — принят не северный (жилые от 2,5 м) (К-7).
См. лист открытых вопросов (лист 7, записи К-1, К-2, К-4, К-7).

Изм.	Кол.уч	Лист	№ док.	Подп.	Дата
Разраб.		Кырлан А.С.			21.10.26
Пров.					
ГИП					
Н. контр.					
Утв.					

ГД-2026-010-АИ

Дом 331 м²

Общая площадь 270,67* м² · * размеры приняты, не замерены (реестр — л. 7, К-1)

Дизайн-проект интерьера

Стадия	Лист	Листов
РП	26	159

Спецификация мебели и оборудования

М б/м

Кырлан Александр Сергеевич

выпуск 18.10.2026 № 9365d64cec · стр. 29 из 197

Спецификация мебели и оборудования (продолжение)

Форма 1 ГОСТ 21.110-2013 · позиции мебели — по плану расстановки

ПРЕДВАРИТЕЛЬНО · не для производства работ · открыто пунктов: 6 (реестр — л. 7)

Поз.	Наименование и техническая характеристика	Тип, марка, обозначение документа, опросного листа	Код продукции	Поставщик	Ед. измерения	Кол.	Масса 1 ед., кг	Примечание
Гс4	Кресло, букле (овечья шерсть); обивка букле, овечья шерсть, молочный; Ш×Г×В 850×850×850 мм			аналог по характеристикам	шт.	1		пом. 5; замена ≤ габарита
Гс5	Кресло-качалка, кожа и ясень; обивка кожа натуральная, тёмный коньяк, дерево — ясень гнутый; Ш×Г×В 850×850×850 мм			аналог по характеристикам	шт.	1		пом. 5; замена ≤ габарита
Гс6	Буфет низкий, дуб; шпон, дуб натуральный, матовое масло; Ш×Г×В 1600×450×800 мм			аналог по характеристикам	шт.	1		пом. 5; крепление к стене; замена ≤ габарита
Кл1	Стеллаж для хранения; каркас и полки — ЛДСП, декор «дуб натуральный»; Ш×Г×В 2600×500×2200 мм			аналог по характеристикам	шт.	1		пом. 7; замена ≤ габарита
Пр2	Банкетка; Ш×Г×В 1000×400×450 мм			аналог по характеристикам	шт.	1		пом. 8; замена ≤ габарита
Гр1	Стеллаж для инструмента и шин; каркас и полки — ЛДСП, декор «дуб натуральный»; Ш×Г×В 3000×500×2000 мм			аналог по характеристикам	шт.	1		пом. 10; крепление к стене; замена ≤ габарита
Гр2	Силовая стойка со скамьёй и штангой; стальная рама, порошковая окраска, чёрный матовый; под тренажёр — резиновый коврик 10 мм; Ш×Г×В 1200×1500×2300 мм			аналог по характеристикам	шт.	1		пом. 10; замена ≤ габарита
Гр3	Верстак с перфопанелью; шпон, дуб натуральный, матовое масло; Ш×Г×В 1800×700×900 мм			аналог по характеристикам	шт.	1		пом. 10; замена ≤ габарита
Гр4	Тренажёр гребной магнитный, складной; алюминиевая направляющая, маховик магнитный или водяной, сиденье на роликах; под тренажёр — резиновый коврик 10 мм; Ш×Г×В 2400×600×500 мм			аналог по характеристикам	шт.	1		пом. 10; замена ≤ габарита
Гр5	Стойка для гантелей 2 яруса, пары 4–20 кг; стальная рама, порошковая окраска, чёрный матовый; гантели с обрезиненными дисками; Ш×Г×В 1000×500×800 мм			аналог по характеристикам	шт.	1		пом. 10; крепление к стене; замена ≤ габарита
Гр6	Стенка шведская, бук, с навесным турником; массив бука, лак матовый; перекладины Ø40 шаг 200; крепление к стене — анкеры по основанию, не менее 6; Ш×Г×В 900×150×2300 мм			аналог по характеристикам	шт.	1		пом. 10; крепление к стене; замена ≤ габарита
Вр1	Стол летний; шпон, дуб натуральный, матовое масло; Ш×Г×В 1600×900×750 мм			аналог по характеристикам	шт.	1		пом. 11; замена ≤ габарита
Вр2	Диван плетёный; обивка — ткань, цвет Tikkurila V451; Ш×Г×В 2000×800×800 мм			аналог по характеристикам	шт.	1		пом. 11; замена ≤ габарита
Вр4, Вр5	Кресло плетёное; обивка — ткань, цвет Tikkurila V451; Ш×Г×В 800×800×800 мм			аналог по характеристикам	шт.	2		пом. 11; замена ≤ габарита
Вр6	Столик кофейный из тика; шпон, дуб натуральный, матовое масло; Ш×Г×В 1000×600×420 мм			аналог по характеристикам	шт.	1		пом. 11; замена ≤ габарита
Вр7	Стул обеденный к столу Вр1; обивка — ткань, цвет Tikkurila V451; каркас — дуб натуральный; Ш×Г×В 450×500×820 мм			аналог по характеристикам	шт.	4		пом. 11; замена ≤ габарита
М1	Кровать 1800×2000, изголовье — мягкое в шерстяном твиде; обивка шерстяной твид, серо-коричневый, дерево — дуб массив, царги и ножки; Ш×Г×В 1800×2100×450 мм			аналог по характеристикам	шт.	1		пом. 13; замена ≤ габарита
М2, М3	Тумба прикроватная, массив ореха; дерево — орех массив, масло; Ш×Г×В 500×400×550 мм			аналог по характеристикам	шт.	2		пом. 13; замена ≤ габарита
М4	Комод, дуб брашированный, фасады с кожаными ручками; дерево — дуб брашированный, масло; Ш×Г×В 1400×500×800 мм			аналог по характеристикам	шт.	1		пом. 13; крепление к стене; замена ≤ габарита
М5	Кресло для чтения, букле (овечья шерсть); обивка букле, овечья шерсть, молочный; Ш×Г×В 800×800×900 мм			аналог по характеристикам	шт.	1		пом. 13; замена ≤ габарита
Гм1	Ящики низкие под скатом (до колена 1200); шпон, дуб натуральный, матовое масло; Ш×Г×В 2600×500×1100 мм			аналог по характеристикам	шт.	1		пом. 14; замена ≤ габарита
Гм2	Система хранения открытая в полную высоту (у перегородки, вне ската); каркас и полки — ЛДСП, декор «дуб натуральный»; Ш×Г×В 1400×500×2400 мм			аналог по характеристикам	шт.	1		пом. 14; замена ≤ габарита
С1	Кровать 1600×2000, изголовье — вертикальная рейка из ясеня; дерево — ясень массив, рейка; Ш×Г×В 1600×2100×450 мм			аналог по характеристикам	шт.	1		пом. 16; замена ≤ габарита
С2	Тумба подвесная, ясень; дерево — ясень шпон; Ш×Г×В 500×400×550 мм			аналог по характеристикам	шт.	1		пом. 16; крепление к стене; замена ≤ габарита
Сп1	Дорожка беговая складная, полотно 1400×500; стальная рама, порошковая окраска, чёрный матовый; под тренажёр резиновый коврик 10 мм; Ш×Г×В 2000×800×1400 мм			аналог по характеристикам	шт.	1		пом. 17; замена ≤ габарита

Допущения и предложения на листе

Основа листа: размеры и контуры этажей подобраны проектировщиком по составу помещений и площадям этажей с картинки 470 px (размеры на ней не читаются); обмер и исходный проект — задание (К-1); высоты: 1-й этаж 2800 мм, мансарда 2700 мм (горизонтальная часть) приняты; скаты кровли мансарды приняты по картинке: колено 1200 мм, уклон 45°, конёк вдоль длинной стороны; проект КР — задание (К-2); наружные стены 400 мм, перегородки 120 мм приняты (К-1); разрешённая мощность 15 кВт принята по типовым ТУ для частного дома (К-4); подрайон климата не задан — принят не северный (жилые от 2,5 м) (К-7).

См. лист открытых вопросов (лист 7, записи К-1, К-2, К-4, К-7).

Изм.	Кол.уч	Лист	№ док.	Подп.	Дата
Разраб.		Кырлан А.С.			21.10.26
Пров.					
ГИП					
Н. контр.					
Утв.					

ГД-2026-010-АИ

Дом 331 м²

Общая площадь 270,67* м² · * размеры приняты, не замерены (реестр — л. 7, К-1)

Дизайн-проект интерьера

Стадия	Лист	Листов
РП	27	159

Спецификация мебели и оборудования (продолжение)

М б/м

Кырлан Александр Сергеевич

Спецификация мебели и оборудования (продолжение)

Форма 1 ГОСТ 21.110-2013 · позиции мебели — по плану расстановки

ПРЕДВАРИТЕЛЬНО · не для производства работ · открыто пунктов: 6 (реестр — л. 7)

Поз.	Наименование и техническая характеристика	Тип, марка, обозначение документа, опросного листа	Код продукции	Поставщик	Ед. измерения	Кол.	Масса 1 ед., кг	Примечание
Сп2	Велотренажёр магнитный; стальная рама, порошковая окраска, чёрный матовый; под тренажёр — резиновый коврик 10 мм; Ш×Г×В 600×1100×1150 мм			аналог по характеристикам	шт.	1		пом. 17; замена ≤ габарита
Сп3	Стеллаж низкий под скатом для книг и инвентаря; каркас и полки — ЛДСП, декор «дуб натуральный»; Ш×Г×В 2400×350×900 мм			аналог по характеристикам	шт.	1		пом. 17; крепление к стене; замена ≤ габарита
Сп4	Стойка-этажерка для инвентаря: гантели 2–8 кг, эспандеры, ролик; стальная рама, порошковая окраска, чёрный матовый; гантели с обрезиненными дисками; Ш×Г×В 500×350×1000 мм			аналог по характеристикам	шт.	1		пом. 17; крепление к стене; замена ≤ габарита
Д1	Кровать 900×2000 с бортиком, массив сосны; дерево — сосна массив, воск; Ш×Г×В 900×2000×450 мм			аналог по характеристикам	шт.	1		пом. 18; замена ≤ габарита
Д2	Стол письменный, столешница ЛДСП светлый ясень, ножки — белая сталь; столешница ЛДСП «светлый ясень», ножки сталь, белая эмаль; Ш×Г×В 1200×600×750 мм			аналог по характеристикам	шт.	1		пом. 18; замена ≤ габарита
Д4	Кровать 900×2000 с ящиками, массив берёзы; дерево — берёза массив, масло; Ш×Г×В 900×2000×450 мм			аналог по характеристикам	шт.	1		пом. 19; замена ≤ габарита
Д5	Стол письменный растущий, берёзовая фанера на регулируемом каркасе; столешница — берёзовая фанера, лак; каркас сталь, тёмно-серая эмаль, регулировка 600–800; Ш×Г×В 1200×600×750 мм			аналог по характеристикам	шт.	1		пом. 19; замена ≤ габарита
	Техника встраиваемая и бытовая, светильники под розетки							
	Посудомоечная машина встраиваемая, в модуле Кх2; ниша 600 мм			аналог по характеристикам	шт.	1		пом. 1; по схеме изготовителя
	Варочная панель встраиваемая, электрическая, в модуле Кх3			аналог по характеристикам	шт.	1		пом. 1; по схеме изготовителя
	Духовой шкаф встраиваемый, в модуле Кх3			аналог по характеристикам	шт.	1		пом. 1; по схеме изготовителя
	Холодильник встраиваемый, в модуле Кх5			аналог по характеристикам	шт.	1		пом. 1; по схеме изготовителя
	Вытяжка встраиваемая, над модулем Кх1			аналог по характеристикам	шт.	1		пом. 1; вывод Р21** (ЭОМ)
	Стиральная машина			аналог по характеристикам	шт.	1		пом. 3; вывод Р7** (ЭОМ)
	Стиральная машина			аналог по характеристикам	шт.	1		пом. 15; вывод Р7** (ЭОМ)
	Стиральная машина, место по листу ВК (Сд4); Ш×Г 600×600 мм			аналог по характеристикам	шт.	1		пом. 20; по схеме изготовителя
	Торшер; абажур — ткань или опаловое стекло; лампа 2700 K			аналог по характеристикам	шт.	1		пом. 5; розетка Р3 (ЭОМ)
	Торшер, у поз. М4; абажур — ткань или опаловое стекло; лампа 2700 K			аналог по характеристикам	шт.	1		пом. 13; розетка Р5 (ЭОМ)
	Текстиль							
Т14	Рулонная штора кассетная, ткань димаут; полиэстер 100 %; цвет NCS S 2005-Y20R; карниз 890 мм, высота 2000 мм			аналог по характеристикам	шт.	1		пом. 1
Т7	Портьеры на люверсах, шерстяной твид; лён 100 %; цвет Farrow & Ball No. 40; карниз 1820 мм, высота 2790 мм, сборка 2			аналог по характеристикам	шт.	2		пом. 2
Т8	Тюль, льняная сетка; полиэстер 100 %; цвет NCS S 0804-Y30R; карниз 1820 мм, высота 2790 мм, сборка 2,5			аналог по характеристикам	шт.	1		пом. 2
Т9	Ковёр джутовый под диваном; шерсть 100 %; цвет Tikkurila X463; 1700×2300 мм			аналог по характеристикам	шт.	1		пом. 2; с подложкой
Т10	Подушки на диван, кожа; букле (шерсть 60 %, полиэстер 40 %); цвет NCS S 3010-Y30R			аналог по характеристикам	шт.	3		пом. 2
Т11	Подушки на кровать, акцент; хлопковый бархат 100 %; цвет Farrow & Ball No. 298			аналог по характеристикам	шт.	2		пом. 2
Т12	Плед на кровать; шерсть мериноса 100 %; цвет Farrow & Ball No. 298			аналог по характеристикам	шт.	1		пом. 2
Т1	Портьеры-волна, два полотна; лён 100 %; цвет NCS S 2005-Y20R; карниз 2150 мм, высота 2710 мм, сборка 2			аналог по характеристикам	шт.	2		пом. 5
Т2	Тюль-вуаль, одно полотно; полиэстер 100 %; цвет NCS S 0804-Y30R; карниз 2150 мм, высота 2710 мм, сборка 2,5			аналог по характеристикам	шт.	1		пом. 5
Т3	Ковёр мягкой группы, шерсть с джутом; шерсть 100 %; цвет Farrow & Ball No. 243; 3600×2400 мм			аналог по характеристикам	шт.	1		пом. 5; с подложкой

Допущения и предложения на листе

Основа листа: размеры и контуры этажей подобраны проектировщиком по составу помещений и площадям этажей с картинки 470 px (размеры на ней не читаются); обмер и исходный проект — задание (К-1); высоты: 1-й этаж 2800 мм, мансарда 2700 мм (горизонтальная часть) приняты; скаты кровли мансарды приняты по картинке: колено 1200 мм, уклон 45°, конёк вдоль длинной стороны; проект КР — задание (К-2); наружные стены 400 мм, перегородки 120 мм приняты (К-1); разрешённая мощность 15 кВт принята по типовым ТУ для частного дома (К-4); подрайон климата не задан — принят не северный (жилые от 2,5 м) (К-7).

Знак «**» — предложение проектировщика, заказчиком не утверждено (согласовать с заказчиком): записи в реестре нет: Р21 — высота 2200 мм выше нормы 1 м (ПУЭ 6.6.30) по назначению: питание вытяжки М25, розетка в модуле за съёмной панелью; Р7 — по образцу: Р7, Р8 и Р33 на высоте 1000 мм — верхний предел нормы (ПУЭ, п. 6.6.30, не выше 1 м); флаг решения снят.

См. лист открытых вопросов (лист 7, записи К-1, К-2, К-4, К-7).

Изм.	Кол.уч	Лист	№ док.	Подп.	Дата
Разраб.		Кырлан А.С.			21.10.26
Пров.					
ГИП					
Н. контр.					
Утв.					

ГД-2026-010-АИ

Дом 331 м²

Общая площадь 270,67* м² · * размеры приняты, не замерены (реестр — л. 7, К-1)

Дизайн-проект интерьера

Стадия	Лист	Листов
РП	28	159

Спецификация мебели и оборудования (продолжение)

М б/м

Кырлан Александр Сергеевич

Спецификация мебели и оборудования (продолжение)

Форма 1 ГОСТ 21.110-2013 · позиции мебели — по плану расстановки

ПРЕДВАРИТЕЛЬНО · не для производства работ · открыто пунктов: 6 (реестр — л. 7)

Поз.	Наименование и техническая характеристика	Тип, марка, обозначение документа, опросного листа	Код продукции	Поставщик	Ед. измерения	Кол.	Масса 1 ед., кг	Примечание
T4	Подушки декоративные на диван, лён; лён 100 %; цвет Farrow & Ball No. 226			аналог по характеристикам	шт.	3		пом. 5
T5	Подушки декоративные на диван, акцент; хлопковый бархат 100 %; цвет Farrow & Ball No. 93			аналог по характеристикам	шт.	2		пом. 5
T6	Плед на диван; шерсть мериноса 100 %; цвет Farrow & Ball No. 93			аналог по характеристикам	шт.	1		пом. 5
T40	Покрытие резиновое модульное 500×500×10 мм под спортзону; резиновая крошка SBR с цветными EPDM-вкраплениями, плиты 500×500, 10 мм; цвет Farrow & Ball No. 243; 1500×6300 мм			аналог по характеристикам	шт.	1		пом. 10
T13	Портьеры-волна, шерсть с блэкаут-подкладкой; лён 100 %; цвет Farrow & Ball No. 229; карниз 1800 мм, высота 2590 мм, сборка 2			аналог по характеристикам	шт.	2		пом. 13
T15	Тюль; полиэстер 100 %; цвет Little Greene No. 105; карниз 1800 мм, высота 2590 мм, сборка 2,5			аналог по характеристикам	шт.	1		пом. 13
T16	Ковёр под кроватью, шерсть ручного ткачества; шерсть 80 %, хлопок 20 %; цвет NCS S 2005-Y20R; 2800×1900 мм			аналог по характеристикам	шт.	1		пом. 13; с подложкой
T17	Подушки декоративные на кровать, шерсть-меланж; лён 100 %; цвет NCS S 2005-Y20R			аналог по характеристикам	шт.	3		пом. 13
T18	Подушки на кровать, акцент; хлопковый бархат 100 %; цвет NCS S 7020-G10Y			аналог по характеристикам	шт.	2		пом. 13
T19	Плед на кровать; шерсть мериноса 100 %; цвет NCS S 7020-G10Y			аналог по характеристикам	шт.	1		пом. 13
T20	Портьеры-волна, хлопок-сатин с блэкаут-подкладкой; лён 100 %; цвет Tikkurila X463; карниз 1820 мм, высота 2690 мм, сборка 2			аналог по характеристикам	шт.	2		пом. 16
T21	Тюль, лён-вуаль; полиэстер 100 %; цвет Little Greene No. 105; карниз 1820 мм, высота 2690 мм, сборка 2,5			аналог по характеристикам	шт.	1		пом. 16
T22	Ковёр под кроватью, шерсть с узором ромбы; шерсть 100 %; цвет NCS S 3010-Y30R; 2000×2500 мм			аналог по характеристикам	шт.	1		пом. 16; с подложкой
T23	Подушки декоративные на кровать, хлопок-рогожка; букле (шерсть 60 %, полиэстер 40 %); цвет Tikkurila X463			аналог по характеристикам	шт.	3		пом. 16
T24	Подушки на кровать, акцент; хлопковый бархат 100 %; цвет Farrow & Ball No. 64			аналог по характеристикам	шт.	2		пом. 16
T25	Плед на кровать; шерсть мериноса 100 %; цвет Farrow & Ball No. 64			аналог по характеристикам	шт.	1		пом. 16
T41	Коврик для йоги и растяжки 1830×610×6, TPE, нескользящий; TPE, 6 мм, двухслойный; цвет NCS S 3020-G30Y; 610×1830 мм			аналог по характеристикам	шт.	1		пом. 17
T26	Портьеры на люверсах, хлопок-канвас с блэкаут-подкладкой; лён 100 %; цвет Tikkurila V451; карниз 1820 мм, высота 2610 мм, сборка 2			аналог по характеристикам	шт.	2		пом. 18
T27	Тюль, хлопковая кисея; полиэстер 100 %; цвет NCS S 0804-Y30R; карниз 1820 мм, высота 2610 мм, сборка 2,5			аналог по характеристикам	шт.	1		пом. 18
T28	Ковёр под кроватью, хлопок, стираемый; шерсть 100 %; цвет NCS S 2005-Y20R; 1600×1200 мм			аналог по характеристикам	шт.	1		пом. 18; с подложкой
T29	Подушки на кровать, хлопок-вельвет; букле (шерсть 60 %, полиэстер 40 %); цвет Tikkurila V451			аналог по характеристикам	шт.	3		пом. 18
T30	Подушки на кровать, акцент; хлопковый бархат 100 %; цвет NCS S 3020-G30Y			аналог по характеристикам	шт.	2		пом. 18
T31	Плед на кровать; шерсть мериноса 100 %; цвет NCS S 3020-G30Y			аналог по характеристикам	шт.	1		пом. 18
T32	Портьеры-волна, лён-меланж с блэкаут-подкладкой; лён 100 %; цвет NCS S 2005-Y20R; карниз 1800 мм, высота 2590 мм, сборка 2			аналог по характеристикам	шт.	2		пом. 19
T33	Тюль, лён-вуаль в мелкую клетку; полиэстер 100 %; цвет Farrow & Ball No. 226; карниз 1800 мм, высота 2590 мм, сборка 2,5			аналог по характеристикам	шт.	1		пом. 19
T34	Ковёр под кроватью, шерсть с узором «горы»; шерсть 100 %; цвет NCS S 3010-Y30R; 1600×1200 мм			аналог по характеристикам	шт.	1		пом. 19; с подложкой
T35	Подушки на кровать, хлопок-канвас с принтом; букле (шерсть 60 %, полиэстер 40 %); цвет Tikkurila X463			аналог по характеристикам	шт.	3		пом. 19
T36	Подушки на кровать, акцент; хлопковый бархат 100 %; цвет NCS S 3040-Y70R			аналог по характеристикам	шт.	2		пом. 19
T37	Плед на кровать; шерсть мериноса 100 %; цвет NCS S 3040-Y70R			аналог по характеристикам	шт.	1		пом. 19

Допущения и предложения на листе

Основа листа: размеры и контуры этажей подобраны проектировщиком по составу помещений и площадям этажей с картинки 470 px (размеры на ней не читаются); обмер и исходный проект — задание (К-1); высоты: 1-й этаж 2800 мм, мансарда 2700 мм (горизонтальная часть) приняты; скаты кровли мансарды приняты по картинке: колено 1200 мм, уклон 45°, конёк вдоль длинной стороны; проект КР — задание (К-2); наружные стены 400 мм, перегородки 120 мм приняты (К-1); разрешённая мощность 15 кВт принята по типовым ТУ для частного дома (К-4); подрайон климата не задан — принят не северный (жилые от 2,5 м) (К-7).

См. лист открытых вопросов (лист 7, записи К-1, К-2, К-4, К-7).

Изм.	Кол.уч	Лист	№ док.	Подп.	Дата
Разраб.		Кырлан А.С.			21.10.26
Пров.					
ГИП					
Н. контр.					
Утв.					

ГД-2026-010-АИ

Дом 331 м²

Общая площадь 270,67* м² · * размеры приняты, не замерены (реестр — л. 7, К-1)

Дизайн-проект интерьера

Стадия	Лист	Листов
РП	29	159

Спецификация мебели и оборудования (продолжение)

М б/м

Кырлан Александр Сергеевич

Спецификация мебели и оборудования (продолжение)

Форма 1 ГОСТ 21.110-2013 · позиции мебели — по плану расстановки

ПРЕДВАРИТЕЛЬНО · не для производства работ · открыто пунктов: 6 (реестр — л. 7)

Поз.	Наименование и техническая характеристика	Тип, марка, обозначение документа, опросного листа	Код продукции	Поставщик	Ед. измерения	Кол.	Масса 1 ед., кг	Примечание
	Декор							
ДК8	Часы настенные Ø400; 400×400 мм; центр на 1550 мм от пола			аналог по характеристикам	шт.	1	2	пом. 1; крепление: дюбель с крюком, 1 точка
ДК9	Хлорофитум хохлатый на подоконнике (отм. +0,800); 300×200 мм; низ на 800 мм от пола			аналог по характеристикам	шт.	1		пом. 1
ДК23	Ваза с тюльпанами на обеденном столе; 200×350 мм; на Кх8			аналог по характеристикам	шт.	1		пом. 1
ДК3	Картина над диваном: офорт в паспарту, рама — орех; 1000×700 мм; низ на 1100 мм от пола			аналог по характеристикам	шт.	1	4	пом. 2; крепление к стене
ДК28	Замиокулькас в кашпо Ø350; 350×350 мм			аналог по характеристикам	шт.	1		пом. 2
ДК1	Картина над буфетом: пейзаж, масло, рама — морёный дуб; 1200×900 мм; низ на 1000 мм от пола			аналог по характеристикам	шт.	1	6	пом. 5; крепление: планка на дюбелях, 4 точки
ДК2	Фикус лировидный в кашпо Ø400; 450×450 мм			аналог по характеристикам	шт.	1		пом. 5
ДК21	Оливковое дерево в кашпо Ø450; 450×450 мм			аналог по характеристикам	шт.	1		пом. 5
ДК22	Ваза с живыми цветами на журнальном столе; 200×350 мм; на Гс3			аналог по характеристикам	шт.	1		пом. 5
ДК5	Зеркало; рама — чёрный матовый; 800×1800 мм; низ на 550 мм от пола			аналог по характеристикам	шт.	1	18	пом. 8; крепление: анкер, 4 шт.
ДК31	Зеркало 1200×1500 для контроля техники, безопасное (плёнка), без рамы; 1200×1500 мм; низ на 600 мм от пола			аналог по характеристикам	шт.	1	22	пом. 10; крепление: анкер, 4 шт.
ДК24	Гортензия крупнолистная в кадке Ø500; 500×500 мм			аналог по характеристикам	шт.	1		пом. 11
ДК25	Самшит в кадке Ø450; 450×450 мм			аналог по характеристикам	шт.	1		пом. 11
ДК26	Папоротник нефролепис в ящике 600×250; 250×600 мм			аналог по характеристикам	шт.	1		пом. 11
ДК4	Картина над кроватью: акварель, рама — лиственница; 1000×700 мм; низ на 1300 мм от пола			аналог по характеристикам	шт.	1	4	пом. 13; крепление к стене
ДК27	Фикус каучуконосный в кашпо Ø400; 400×400 мм			аналог по характеристикам	шт.	1		пом. 13
ДК6	Картина над кроватью: натюрморт, масло, рама — тонкая латунь; 1000×700 мм; низ на 1300 мм от пола			аналог по характеристикам	шт.	1	4	пом. 16; крепление к стене
ДК7	Зеркало в рост в раме из ясеня; рама — чёрный матовый; 600×1600 мм; низ на 300 мм от пола			аналог по характеристикам	шт.	1	12	пом. 16; крепление: анкер для пустотелых оснований, 4 шт.
ДК30	Монстера в кашпо Ø450 с фитолампой; 450×450 мм			аналог по характеристикам	шт.	1		пом. 17
ДК10	Картина над кроватью: детская иллюстрация, рама — светлый ясень; 600×700 мм; низ на 1100 мм от пола			аналог по характеристикам	шт.	1	4	пом. 18; крепление к стене
ДК11	Зеркало безопасное (плёнка), рама — светлый ясень; рама — чёрный матовый; 500×1600 мм; низ на 300 мм от пола			аналог по характеристикам	шт.	1	12	пом. 18; крепление: анкер для пустотелых оснований, 4 шт.
ДК12	Картина над кроватью: детский принт, рама — белёный дуб; 600×700 мм; низ на 1100 мм от пола			аналог по характеристикам	шт.	1	4	пом. 19; крепление к стене
ДК13	Зеркало круглое Ø600 в кожаном ремне; рама — чёрный матовый; 600×600 мм; низ на 1150 мм от пола			аналог по характеристикам	шт.	1	12	пом. 19; крепление: анкер для пустотелых оснований, 4 шт.

Допущения и предложения на листе

Основа листа: размеры и контуры этажей подобраны проектировщиком по составу помещений и площадям этажей с картинки 470 px (размеры на ней не читаются); обмер и исходный проект — задание (К-1); высоты: 1-й этаж 2800 мм, мансарда 2700 мм (горизонтальная часть) приняты; скаты кровли мансарды приняты по картинке: колено 1200 мм, уклон 45°, конёк вдоль длинной стороны; проект КР — задание (К-2); наружные стены 400 мм, перегородки 120 мм приняты (К-1); разрешённая мощность 15 кВт принята по типовым ТУ для частного дома (К-4); подрайон климата не задан — принят не северный (жилые от 2,5 м) (К-7).

См. лист открытых вопросов (лист 7, записи К-1, К-2, К-4, К-7).

Изм.	Кол.уч	Лист	№ док.	Подп.	Дата
Разраб.		Кырлан А.С.			21.10.26
Пров.					
ГИП					
Н. контр.					
Утв.					

ГД-2026-010-АИ

Дом 331 м²

Общая площадь 270,67* м² · * размеры приняты, не замерены (реестр — л. 7, К-1)

Дизайн-проект интерьера

Стадия	Лист	Листов
РП	30	159

Спецификация мебели и оборудования (продолжение)

М б/м

Кырлан Александр Сергеевич

План розеток и электровыводов · 1-й этаж

Розетки, выводы кабеля, щит · размеры в мм · высоты от чистого пола

ПРЕДВАРИТЕЛЬНО · не для производства работ · открыто пунктов: 6 (реестр — л. 7)

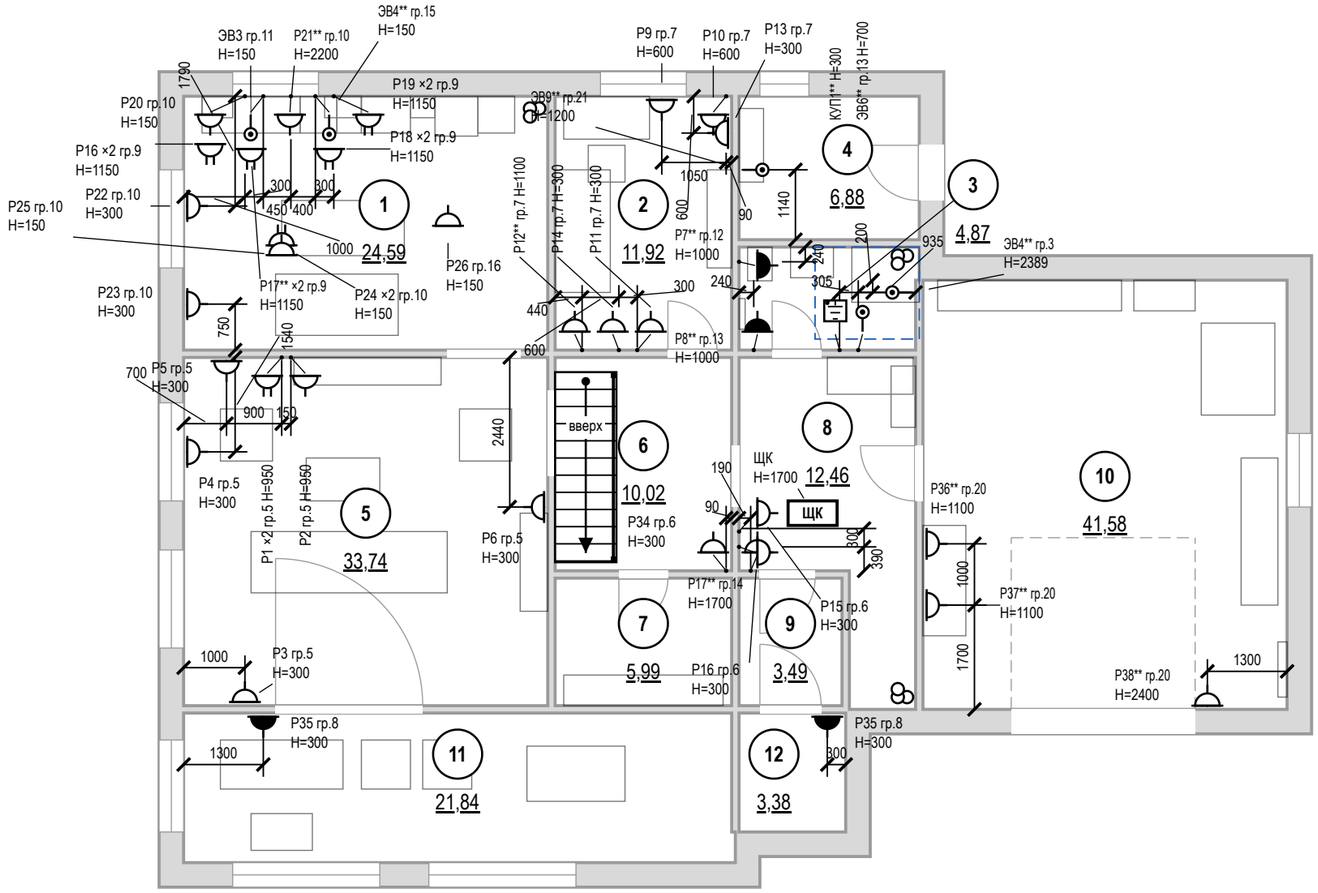

Условные обозначения

- розетка с заземляющим контактом; у знака — марка, ×N постов в рамке, гр. — группа щита, H — высота оси, мм
- то же, рамка на 2 поста (число черточек — число постов)
- розетка влагозащищённая IP44
- вывод кабеля для подключения прибора (без розетки), марка ЭВ
- КУП — коробка уравнивания потенциалов (ДСУП), проводник к шине PE щита
- ЩК — щит квартирный
- знак разведён для читаемости: точка на стене — у выноски, привязка — до неё
- граница зоны 2 ванной (600 мм от ванны/поддона)
- мебель и сантехприборы — подложка
- стояк: К1 — канализация, В1 — ХВС, Т3 — ГВС
- 1 — номер помещения, площадь м²

Допущения и предложения на листе

Основа листа: размеры и контуры этажей подобраны проектировщиком по составу помещений и площадям этажей с картинки 470 px (размеры на ней не читаются); обмер и исходный проект — задание (К-1); высоты: 1-й этаж 2800 мм, мансарда 2700 мм (горизонтальная часть) приняты; скаты кровли мансарды приняты по картинке: колено 1200 мм, уклон 45°, конёк вдоль длинной стороны; проект КР — задание (К-2); наружные стены 400 мм, перегородки 120 мм приняты (К-1); разрешённая мощность 15 кВт принята по типовым ТУ для частного дома (К-4); подрайон климата не задан — принят не северный (жилые от 2,5 м) (К-7).

Знак «**» — предложение проектировщика, заказчиком не утверждено (согласовать с заказчиком): записи в реестре нет: P21 — высота 2200 мм выше нормы 1 м (ПУЭ 6.6.30) по назначению: питание вытяжки M25, розетка в модуле за съёмной панелью; P12 — высота 1100 мм выше нормы 1 м (ПУЭ 6.6.30) по назначению: питание ТВ над комодом, в одной зоне с выводами TB2 и LAN2; P7, P8 — по образцу: P7, P8 и P33 на высоте 1000 мм — верхний предел нормы (ПУЭ, п. 6.6.30, не выше 1 м); флаг решения снят; ЭВ4, КУП1 — по образцу: Добавлены выводы к вентиляторам: ЭВ4 (ВР1, ванная) и ЭВ5 (ВР3, санузел 2) — группа 3, высота 2389 мм, включение с основным светом, таймер выбега в вентиляторе; и коробки уравнивания потенциалов КУП1 (ванная) и КУП2 (санузел 2) — высота 300 мм, у входа, вне зон 0–2, проводник от шины PE щита ЩК, сече; ЭВ6 — по образцу: Добавлены электрические полотенцесушители IP44: П10 в ванной (480 мм, низ 900 мм) и П13 в санузле 2 (400 мм, низ 900 мм), выводы ЭВ6 и ЭВ7; мощность группы 13 — 2,4 кВт вместо 1,8 кВт; ЭВ9 — место и тип котла не выбраны (газ / электро — вопрос заказчику): вывод у стены D, уточнить по проекту котельной; P17 — высота 1700 мм выше нормы 1 м (ПУЭ 6.6.30) по назначению: питание слаботочного щита ЩС, рядом со щитом на его высоте; P36, P37 — высота 1100 мм выше 1 м по назначению: над столешницей верстака 900 мм; P38 — высота 2400 мм выше 1 м по назначению: питание привода ворот у его места на потолке.

Открытые вопросы и конфликты по листу: К-4.

См. лист открытых вопросов (лист 7, записи К-1, К-2, К-4, К-7).

Примечания

1. За отметку 0,000 принят уровень чистого пола. Высоты H — от чистого пола до оси изделия; привязки — от чистовой грани стены до оси механизма (у рамки на несколько постов — до оси рамки).
2. Высота установки, не указанная на плане: розетки — 300 мм от чистого пола; выводы кабеля — по паспорту прибора.
3. Розетки в санузле — только вне зон 0–2 (ПУЭ 7.1.48, ГОСТ Р 50571.7.701-2024), IP44, через УЗО 30 мА.
4. Розеточные и мокрые линии — через УЗО или дифавтомат с током утечки не более 30 мА (ПУЭ 7.1.79); в санузле выполнить ДСУП (ПУЭ 7.1.87–7.1.88).
5. Кабель — медный, исполнение нг(A)-LS (ГОСТ 31565-2012); скрытая прокладка только горизонтально и вертикально, фактические трассы зафиксировать исполнительной схемой до закрытия отделкой.
6. Расчёт нагрузок, токов КЗ, селективности и сечений — по проекту ЭОМ организации с допуском СРО; лист задаёт состав, расположение и группы.
7. Выводы кухонной техники — после утверждения проекта кухни (ориентировочно); привязки выводов даны от осей модулей гарнитура и пересматриваются вместе с проектом кухни.
8. Электрический тёплый пол проектом не предусмотрен; при решении заказчика устроить — отдельный лист «План тёплых полов»: контуры с отступом 100 мм от стен и мебели без ножек, датчик в гофре, терморегулятор, своя группа щита через УЗО 30 мА.
9. Ведомости электроточек, изделий, светильников и расшифровка клавиш — лист 37.

1000 мм · печать 1:1

Изм.	Кол.уч	Лист	№ док.	Подп.	Дата
Разраб.		Кырлан А.С.			21.10.26
Пров.					
ГИП					
Н. контр.					
Утв.					

ГД-2026-010-АИ

Дом 331 м²

Общая площадь 270,67* м² · * размеры приняты, не замерены (реестр — л. 7, К-1)

Дизайн-проект интерьера

Стадия	Лист	Листов
РП	31	159

План розеток и электровыводов · 1-й этаж

М 1:100

Кырлан Александр Сергеевич

выпуск 18.10.2026 № 9365d64cec · стр. 34 из 197

План розеток и электровыводов · Мансарда

Розетки, выводы кабеля, щит · размеры в мм · высоты от чистого пола

ПРЕДВАРИТЕЛЬНО · не для производства работ · открыто пунктов: 6 (реестр — л. 7)

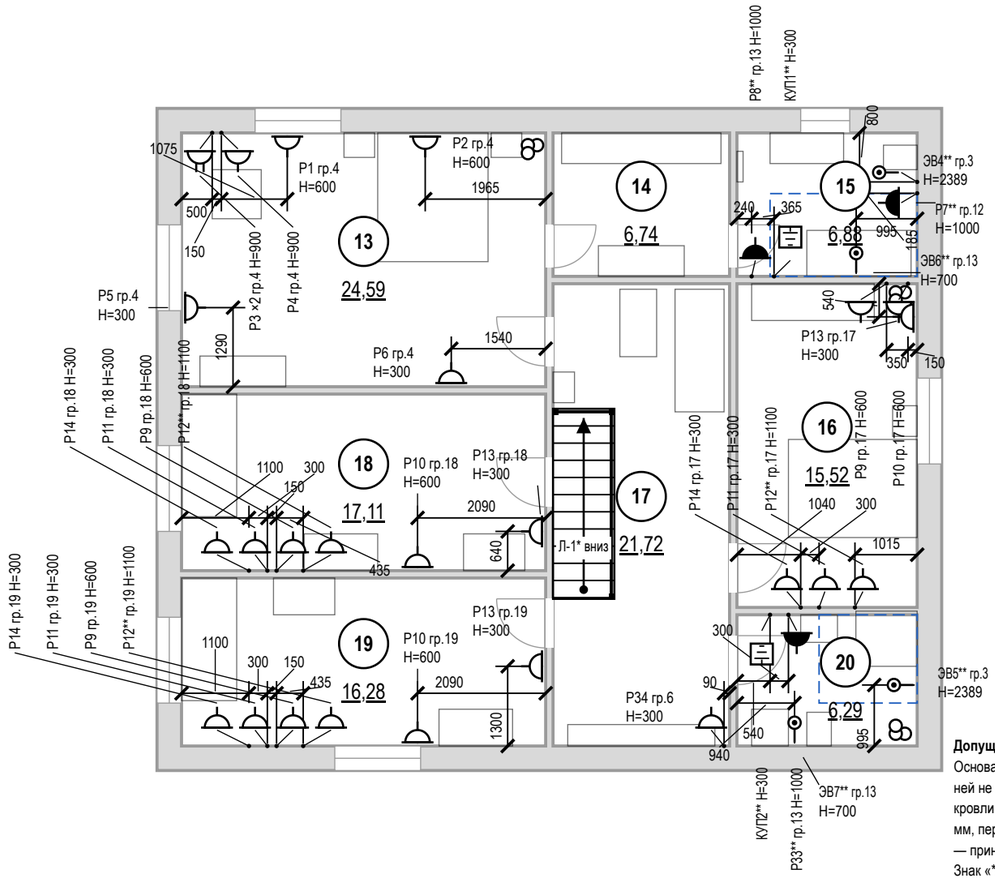

Условные обозначения

- розетка с заземляющим контактом; у знака — марка, ×N постов в рамке, гр. — группа щита, Н — высота оси, мм
- то же, рамка на 2 поста (число черточек — число постов)
- розетка влагозащищённая IP44
- вывод кабеля для подключения прибора (без розетки), марка ЭВ
- КУП — коробка уравнивания потенциалов (ДСУП), проводник к шине РЕ щита
- знак разведён для читаемости: точка на стене — у выноски, привязка — до неё
- граница зоны 2 ванной (600 мм от ванны/поддона)
- мебель и сантехприборы — подложка
- стояк: К1 — канализация, В1 — ХВС, Т3 — ГВС
- 1 — номер помещения, площадь м²

Допущения и предложения на листе

Основа листа: размеры и контуры этажей подобраны проектировщиком по составу помещений и площадям этажей с картинки 470 px (размеры на ней не читаются); обмер и исходный проект — задание (К-1); высоты: 1-й этаж 2800 мм, мансарда 2700 мм (горизонтальная часть) приняты; скаты кровли мансарды приняты по картинке: колено 1200 мм, уклон 45°, конёк вдоль длинной стороны; проект КР — задание (К-2); наружные стены 400 мм, перегородки 120 мм приняты (К-1); разрешённая мощность 15 кВт принята по типовым ТУ для частного дома (К-4); подрайон климата не задан — принят не северный (жилые от 2,5 м) (К-7).

Знак «*» — принято, не замерено и не подтверждено (замерить на объекте): К-6: Л-1 — габарит марша снят с картинки заказчика (11 проступей в холле 3,6 м), а до отм. +3,150 нужно 18 подъёмов — одномаршевая не встаёт: решение по К-6.

Знак «**» — предложение проектировщика, заказчиком не утверждено (согласовать с заказчиком): записи в реестре нет: Р12 — высота 1100 мм выше нормы 1 м (ПУЭ 6.6.30) по назначению: питание ТВ над комодом, в одной зоне с выводами ТВ2 и LAN2; Р7, Р8 — по образцу: Р7, Р8 и Р33 на высоте 1000 мм — верхний предел нормы (ПУЭ, п. 6.6.30, не выше 1 м); флаг решения снят; ЭВ4, КУП1, ЭВ5, КУП2 — по образцу: Добавлены выводы к вентиляторам: ЭВ4 (ВР1, ванная) и ЭВ5 (ВР3, санузел 2) — группа 3, высота 2389 мм, включение с основным светом, таймер выбега в вентиляторе; и коробки уравнивания потенциалов КУП1 (ванная) и КУП2 (санузел 2) — высота 300 мм, у входа, вне зон 0–2, проводник от шины РЕ щита ЩК, сече; ЭВ6, ЭВ7 — по образцу: Добавлены электрические полотенцесушители IP44: П10 в ванной (480 мм, низ 900 мм) и П13 в санузле 2 (400 мм, низ 900 мм), выводы ЭВ6 и ЭВ7; мощность группы 13 — 2,4 кВт вместо 1,8 кВт; Р33 — по образцу: Розетка Р33 на высоте 1100 мм, вне шва плитки.

Открытые вопросы и конфликты по листу: К-4.

См. лист открытых вопросов (лист 7, записи К-1, К-2, К-4, К-6, К-7).

Примечания

1. За отметку 0,000 принят уровень чистого пола. Высоты Н — от чистого пола до оси изделия; привязки — от чистовой грани стены до оси механизма (у рамки на несколько постов — до оси рамки).
2. Высота установки, не указанная на плане: розетки — 300 мм от чистого пола; выводы кабеля — по паспорту прибора.
3. Розетки в санузле — только вне зон 0–2 (ПУЭ 7.1.48, ГОСТ Р 50571.7.701-2024), IP44, через УЗО 30 мА.
4. Розеточные и мокрые линии — через УЗО или дифавтомат с током утечки не более 30 мА (ПУЭ 7.1.79); в санузле выполнить ДСУП (ПУЭ 7.1.87–7.1.88).
5. Кабель — медный, исполнение нг(А)-LS (ГОСТ 31565-2012); скрытая прокладка только горизонтально и вертикально, фактические трассы зафиксировать исполнительной схемой до закрытия отделкой.
6. Расчёт нагрузок, токов КЗ, селективности и сечений — по проекту ЭОМ организации с допуском СРО; лист задаёт состав, расположение и группы.
7. Электрический тёплый пол проектом не предусмотрен; при решении заказчика устроить — отдельный лист «План тёплых полов»: контуры с отступом 100 мм от стен и мебели без ножек, датчик в гофре, терморегулятор, своя группа щита через УЗО 30 мА.
8. Ведомости электроточек, изделий, светильников и расшифровка клавиш — лист 37.

1000 мм · печать 1:1

Изм.	Кол.уч	Лист	№ док.	Подп.	Дата
Разраб.		Кырлан А.С.			21.10.26
Пров.					
ГИП					
Н. контр.					
Утв.					

ГД-2026-010-АИ

Дом 331 м²

Общая площадь 270,67* м² · * размеры приняты, не замерены (реестр — л. 7, К-1)

Дизайн-проект интерьера

Стадия	Лист	Листов
РП	32	159

План розеток и электровыводов · Мансарда

М 1:100

Кырлан Александр Сергеевич

План освещения · 1-й этаж

Светильники, группы включения, извещатели · размеры в мм

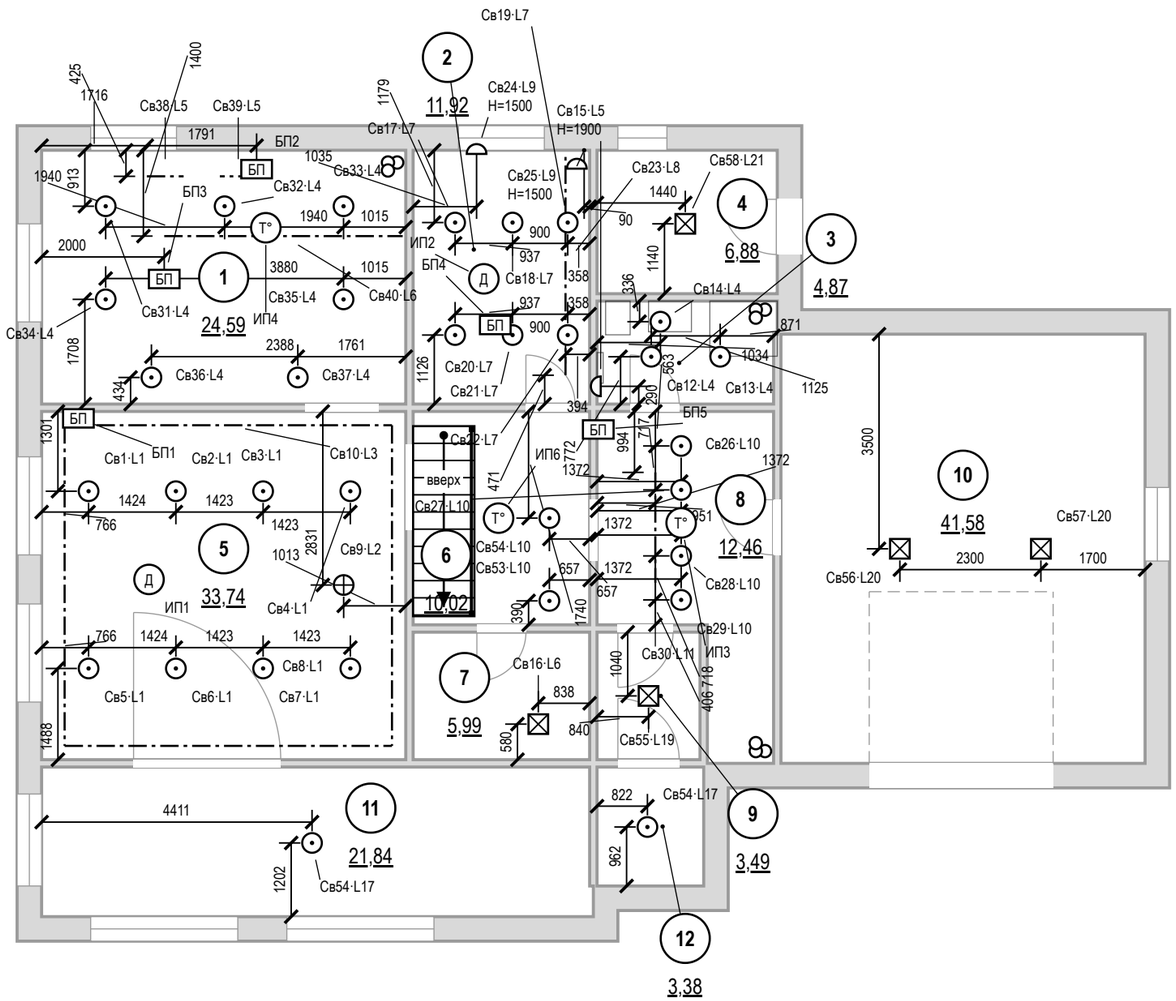

Условные обозначения

- светильник встраиваемый точечный
- светильник потолочный накладной
- светильник подвесной
- светильник настенный (бра), H — высота оси
- светодиодная лента в профиле / в карнизе короба
- Св1·L1 — марка светильника (как в ведомости и на развёртках) · группа включения L (лист выключателей)
- Д — извещатель пожарный дымовой автономный
- Т° — извещатель пожарный тепловой
- БП — блок питания LED, с доступом (люк от 100×100 мм)
- 1 — номер помещения, площадь м²

Освещённость (оценка)

Пом.	S, м²	Ен, лк	Ф треб., лм	Ф по пр., лм
1	24,6	150	10390	7000
2	11,9	300	10070	6300
3	4,9	50	690	1500
4	6,9	30	580	900
5	33,7	150	14260	8000
6	10	50	1410	1200
7	6	30	510	900
8	12,5	50	1750	2400
9	3,5	50	490	900
10	41,6	30	3510	5000

Допущения и предложения на листе

Основа листа: размеры и контуры этажей подобраны проектировщиком по составу помещений и площадям этажей с картинки 470 px (размеры на ней не читаются); обмер и исходный проект — задание (К-1); высоты: 1-й этаж 2800 мм, мансарда 2700 мм (горизонтальная часть) приняты; скаты кровли мансарды приняты по картинке: колено 1200 мм, уклон 45°, конёк вдоль длинной стороны; проект КР — задание (К-2); наружные стены 400 мм, перегородки 120 мм приняты (К-1); разрешённая мощность 15 кВт принята по типовым ТУ для частного дома (К-4); подрайон климата не задан — принят не северный (жилые от 2,5 м) (К-7).

См. лист открытых вопросов (лист 7, записи К-1, К-2, К-4, К-7).

Примечания

1. За отметку 0,000 принят уровень чистого пола. Высоты H — от чистого пола до оси изделия; привязки — от чистовой грани стены до оси механизма (у рамки на несколько постов — до оси рамки).
2. Высота установки, не указанная на плане: светильники — на потолке; настенные — по отметке H у знака. Привязки — до оси светильника от чистовой грани стены, по рядам.
3. Освещённость: Ен — СанПиН 1.2.3685-21, табл. 5.52 (на полу); Ф треб. = Ен·S/(U·MF) при U = 0,5 и MF = 0,71 (СП 52.13330.2016, табл. 4.3) — оценка, не светотехнический расчёт. Декоративная подсветка в Ф не входит.
4. Во влажных помещениях — светильники не ниже IP44; в зонах 0–2 ванной — по ГОСТ Р 50571.7.701-2024 (зона 1 — IPX5).
5. LED-лента в карнизе подсветки короба — по линии карниза с плана потолков; блок питания — в люке короба (БП на плане), питание ленты длиннее 5 м — с двух концов.
6. Розеточные и мокрые линии — через УЗО или дифавтомат с током утечки не более 30 мА (ПУЭ 7.1.79); в санузле выполнить ДСУП (ПУЭ 7.1.87–7.1.88).
7. Кабель — медный, исполнение нг(A)-LS (ГОСТ 31565-2012); скрытая прокладка только горизонтально и вертикально, фактические трассы зафиксировать исполнительной схемой до закрытия отделкой.
8. Расчёт нагрузок, токов КЗ, селективности и сечений — по проекту ЭОМ организации с допуском СРО; лист задаёт состав, расположение и группы.
9. Ведомость светильников — лист 37.

1000 мм · печать 1:1

Изм.	Кол.уч	Лист	№ док.	Подп.	Дата
Разраб.		Кырлан А.С.			21.10.26
Пров.					
ГИП					
Н. контр.					
Утв.					

ГД-2026-010-АИ

Дом 331 м²

Общая площадь 270,67* м² · * размеры приняты, не замерены (реестр — л. 7, К-1)

Дизайн-проект интерьера

Стадия	Лист	Листов
РП	33	159

План освещения · 1-й этаж

М 1:100

Кырлан Александр Сергеевич

выпуск 18.10.2026 № 9365d64cec · стр. 36 из 197

План освещения · Мансарда

Светильники, группы включения, извещатели · размеры в мм

ПРЕДВАРИТЕЛЬНО · не для производства работ · открыто пунктов: 6 (реестр — л. 7)

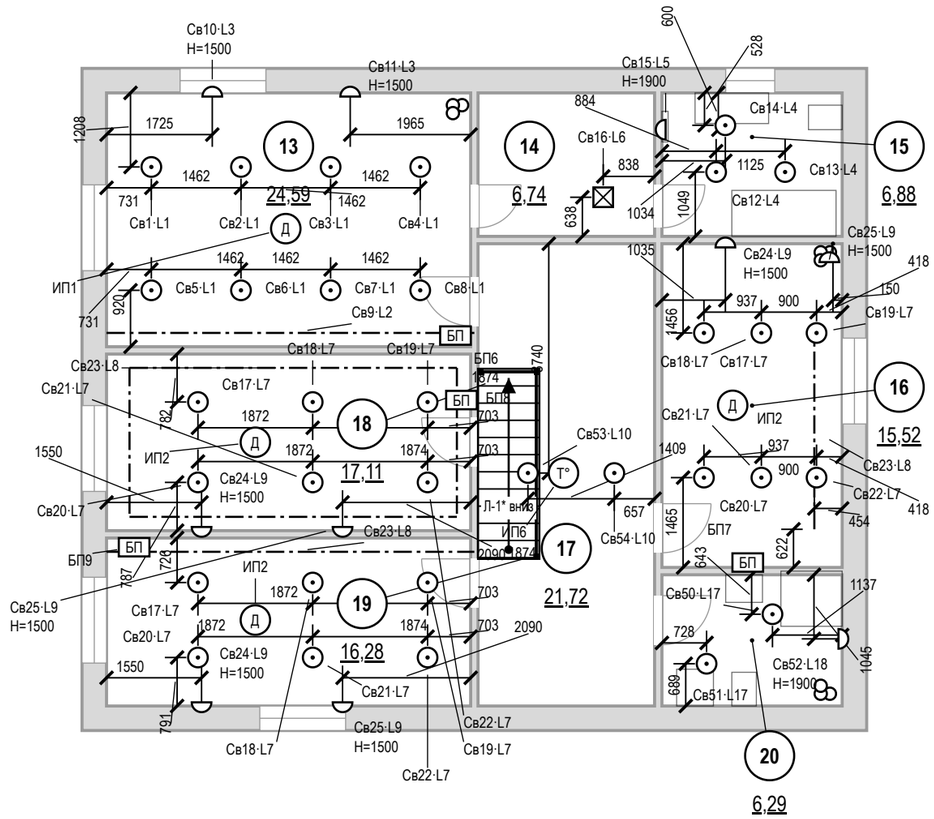

Допущения и предложения на листе

Основа листа: размеры и контуры этажей подобраны проектировщиком по составу помещений и площадям этажей с картинки 470 px (размеры на ней не читаются); обмер и исходный проект — задание (К-1); высоты: 1-й этаж 2800 мм, мансарда 2700 мм (горизонтальная часть) приняты; скаты кровли мансарды приняты по картинке: колено 1200 мм, уклон 45°, конёк вдоль длинной стороны; проект КР — задание (К-2); наружные стены 400 мм, перегородки 120 мм приняты (К-1); разрешённая мощность 15 кВт принята по типовым ТУ для частного дома (К-4); подрайон климата не задан — принят не северный (жилые от 2,5 м) (К-7).

Знак «*» — принято, не замерено и не подтверждено (замерить на объекте): К-6: Л-1 — габарит марша снят с картинки заказчика (11 проступей в холле 3,6 м), а до отм. +3,150 нужно 18 подъёмов — одномаршевая не встаёт: решение по К-6.

См. лист открытых вопросов (лист 7, записи К-1, К-2, К-4, К-6, К-7).

Примечания

1. За отметку 0,000 принят уровень чистого пола. Высоты Н — от чистого пола до оси изделия; привязки — от чистовой грани стены до оси механизма (у рамки на несколько постов — до оси рамки).
2. Высота установки, не указанная на плане: светильники — на потолке; настенные — по отметке Н у знака. Привязки — до оси светильника от чистовой грани стены, по рядам.
3. Освещённость: Ен — СанПиН 1.2.3685-21, табл. 5.52 (на полу); Ф треб. = Ен·S/(U·MF) при U = 0,5 и MF = 0,71 (СП 52.13330.2016, табл. 4.3) — оценка, не светотехнический расчёт. Декоративная подсветка в Ф не входит.
4. Во влажных помещениях — светильники не ниже IP44; в зонах 0–2 ванной — по ГОСТ Р 50571.7.701-2024 (зона 1 — IPX5).
5. LED-лента в карнизе подсветки короба — по линии карниза с плана потолков; блок питания — в люке короба (БП на плане), питание ленты длиннее 5 м — с двух концов.
6. Розеточные и мокрые линии — через УЗО или дифавтомат с током утечки не более 30 мА (ПУЭ 7.1.79); в санузле выполнить ДСУП (ПУЭ 7.1.87–7.1.88).
7. Кабель — медный, исполнение нг(А)-LS (ГОСТ 31565-2012); скрытая прокладка только горизонтально и вертикально, фактические трассы зафиксировать исполнительной схемой до закрытия отделкой.
8. Расчёт нагрузок, токов КЗ, селективности и сечений — по проекту ЭОМ организации с допуском СРО; лист задаёт состав, расположение и группы.
9. Ведомость светильников — лист 37.

1000 мм · печать 1:1

Условные обозначения

- светильник встраиваемый точечный
- светильник потолочный накладной
- светильник настенный (бра), Н — высота оси
- светодиодная лента в профиле / в карнизе короба
- Св1·L1 — марка светильника (как в ведомости и на развёртках) · группа включения L (лист выключателей)
- Д — извещатель пожарный дымовой автономный
- Т° — извещатель пожарный тепловой
- БП — блок питания LED, с доступом (люк от 100×100 мм)
- 1 — номер помещения, площадь м²

Освещённость (оценка)

Пом.	S, м²	Ен, лк	Ф треб., лм	Ф по пр., лм
13	24,6	150	10390	8000
14	6,7	75	1420	900
15	6,9	50	970	1500
16	15,5	150	6560	6300
17	21,7	50	3060	1200
18	17,1	200	9640	6300
19	16,3	200	9170	6300
20	6,3	50	890	1100

Изм.	Кол.уч	Лист	№ док.	Подп.	Дата
Разраб.		Кырлан А.С.			21.10.26
Пров.					
ГИП					
Н. контр.					
Утв.					

ГД-2026-010-АИ

Дом 331 м²

Общая площадь 270,67* м² · * размеры приняты, не замерены (реестр — л. 7, К-1)

Дизайн-проект интерьера

Стадия	Лист	Листов
РП	34	159

План освещения · Мансарда

М 1:100

Кырлан Александр Сергеевич

выпуск 18.10.2026 № 9365d64cec · стр. 37 из 197

План выключателей и схема включения · 1-й этаж

Выключатели S, группы включения L, линии связи · размеры в мм

ПРЕДВАРИТЕЛЬНО · не для производства работ · открыто пунктов: 6 (реестр — л. 7)

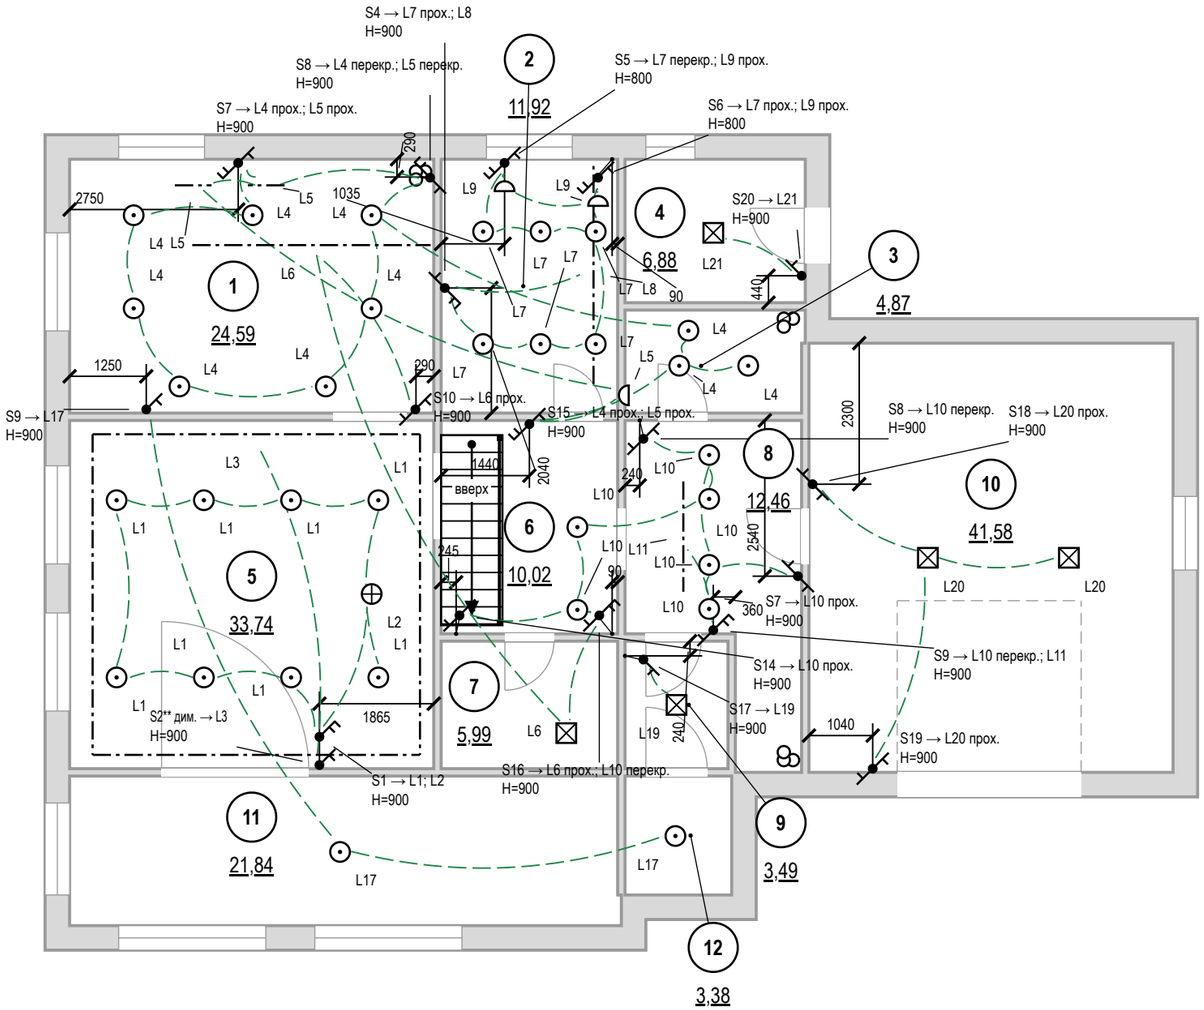

Условные обозначения

- выключатель одноклавишный
- выключатель двухклавишный (флажков — по числу клавиш)
- выключатель с проходной или перекрёстной клавишей (обратный флажок); тип клавиши — в подписи
- S1 → — марка → группы по клавишам (через «;»): прох. — проходной, перекр. — перекрёстный, дим. — светорегулятор; Н — высота
- линия связи: выключатель → светильники группы (не трасса кабеля)
- светильник встраиваемый точечный
- светильник потолочный накладной
- светильник подвесной
- светильник настенный (бра), Н — высота оси
- светодиодная лента в профиле / в карнизе короба
- L1 — группа включения у светильника
- (1) — номер помещения, площадь м²

Допущения и предложения на листе

Основа листа: размеры и контуры этажей подобраны проектировщиком по составу помещений и площадям этажей с картинки 470 px (размеры на ней не читаются); обмер и исходный проект — задание (К-1); высоты: 1-й этаж 2800 мм, мансарда 2700 мм (горизонтальная часть) приняты; скаты кровли мансарды приняты по картинке: колено 1200 мм, уклон 45°, конёк вдоль длинной стороны; проект КР — задание (К-2); наружные стены 400 мм, перегородки 120 мм приняты (К-1); разрешённая мощность 15 кВт принята по типовым ТУ для частного дома (К-4); подрайон климата не задан — принят не северный (жилые от 2,5 м) (К-7).

Знак «**» — предложение проектировщика, заказчиком не утверждено (согласовать с заказчиком): записи в реестре нет: S2 — светорегулятор добавлен под диммируемую ленту L3; уровни сценариев выбраны конвейером.

См. лист открытых вопросов (лист 7, записи К-1, К-2, К-4, К-7).

Примечания

1. За отметку 0,000 принят уровень чистого пола. Высоты Н — от чистого пола до оси изделия; привязки — от чистовой грани стены до оси механизма (у рамки на несколько постов — до оси рамки).
2. Высота установки, не указанная на плане: выключатели — 900 мм от чистого пола, со стороны дверной ручки (ПУЭ 7.1.51).
3. Линии связи показывают, какой выключатель какую группу L включает; это не трасса кабеля. Трасса — принципиальная, фактическую зафиксировать исполнительной схемой.
4. Группы из нескольких мест (L4 — S7, S8, S15; L5 — S7, S8, S15; L6 — S10, S16; L7 — S4, S5, S6; L9 — S5, S6; L10 — S7, S8, S9, S14, S16; L20 — S18, S19): на крайних местах — проходные клавиши, на промежуточных — перекрёстные; механизмы — в ведомости изделий.
5. Светорегулятор — по заднему фронту (для LED-драйверов), совместимость с драйверами проверить до закупки.
6. Розеточные и мокрые линии — через УЗО или дифавтомат с током утечки не более 30 мА (ПУЭ 7.1.79); в санузле выполнить ДСУП (ПУЭ 7.1.87–7.1.88).
7. Кабель — медный, исполнение нг(А)-LS (ГОСТ 31565-2012); скрытая прокладка только горизонтально и вертикально, фактические трассы зафиксировать исполнительной схемой до закрытия отделкой.
8. Расчёт нагрузок, токов КЗ, селективности и сечений — по проекту ЭОМ организации с допуском СРО; лист задаёт состав, расположение и группы.
9. Расшифровка клавиш и ведомость изделий — лист 37.

1000 мм · печать 1:1

Изм.	Кол.уч	Лист	№ док.	Подп.	Дата
Разраб.		Кырлан А.С.			21.10.26
Пров.					
ГИП					
Н. контр.					
Утв.					

ГД-2026-010-АИ

Дом 331 м²

Общая площадь 270,67* м² · * размеры приняты, не замерены (реестр — л. 7, К-1)

Дизайн-проект интерьера

Стадия	Лист	Листов
РП	35	159

План выключателей и схема включения · 1-й этаж

М 1:100

Кырлан Александр Сергеевич

выпуск 18.10.2026 № 9365d64cec · стр. 38 из 197

План выключателей и схема включения · Мансарда

Выключатели S, группы включения L, линии связи · размеры в мм

ПРЕДВАРИТЕЛЬНО · не для производства работ · открыто пунктов: 6 (реестр — л. 7)

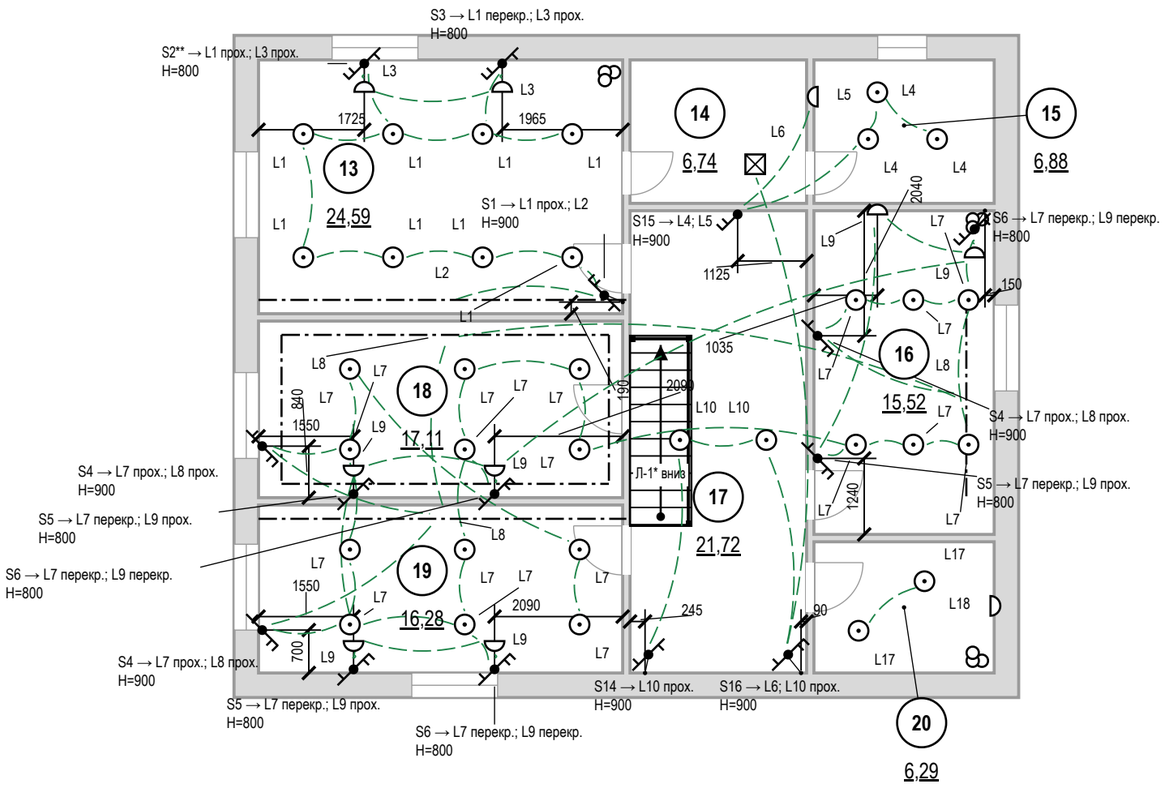

Условные обозначения

- выключатель двухклавишный (флажков — по числу клавиш)
- выключатель с проходной или перекрёстной клавишей (обратный флажок); тип клавиши — в подписи
- S1 → — марка → группы по клавишам (через «;»): прох. — проходной, перекр. — перекрёстный, дим. — светорегулятор; H — высота
- линия связи: выключатель → светильники группы (не трасса кабеля)
- светильник встраиваемый точечный
- светильник потолочный накладной
- светильник настенный (бра), H — высота оси
- светодиодная лента в профиле / в карнизе короба
- L1 — группа включения у светильника
- 1 — номер помещения, площадь м²

Допущения и предложения на листе

Основа листа: размеры и контуры этажей подобраны проектировщиком по составу помещений и площадям этажей с картинки 470 px (размеры на ней не читаются); обмер и исходный проект — задание (К-1); высоты: 1-й этаж 2800 мм, мансарда 2700 мм (горизонтальная часть) приняты; скаты кровли мансарды приняты по картинке: колено 1200 мм, уклон 45°, конёк вдоль длинной стороны; проект КР — задание (К-2); наружные стены 400 мм, перегородки 120 мм приняты (К-1); разрешённая мощность 15 кВт принята по типовым ТУ для частного дома (К-4); подрайон климата не задан — принят не северный (жилые от 2,5 м) (К-7).

Знак «*» — принято, не замерено и не подтверждено (замерить на объекте): К-6: Л-1 — габарит марша снят с картинки заказчика (11 проступей в холле 3,6 м), а до отм. +3,150 нужно 18 подъёмов — одномаршевая не встаёт: решение по К-6.

Знак «**» — предложение проектировщика, заказчиком не утверждено (согласовать с заказчиком): записи в реестре нет: S2 — светорегулятор добавлен под диммируемую ленту L3; уровни сценариев выбраны конвейером.

См. лист открытых вопросов (лист 7, записи К-1, К-2, К-4, К-6, К-7).

Примечания

1. За отметку 0,000 принят уровень чистого пола. Высоты H — от чистого пола до оси изделия; привязки — от чистовой грани стены до оси механизма (у рамки на несколько постов — до оси рамки).
2. Высота установки, не указанная на плане: выключатели — 900 мм от чистого пола, со стороны дверной ручки (ПУЭ 7.1.51).
3. Линии связи показывают, какой выключатель какую группу L включает; это не трасса кабеля. Трасса — принципиальная, фактическую зафиксировать исполнительной схемой.
4. Группы из нескольких мест (L1 — S1, S2**, S3; L3 — S2**, S3; L7 — S4, S4, S4, S5, S5, S5, S6, S6, S6; L8 — S4, S4, S4; L9 — S5, S5, S5, S6, S6, S6; L10 — S14, S16): на крайних местах — проходные клавиши, на промежуточных — перекрёстные; механизмы — в ведомости изделий.
5. Розеточные и мокрые линии — через УЗО или дифавтомат с током утечки не более 30 мА (ПУЭ 7.1.79); в санузле выполнить ДСУП (ПУЭ 7.1.87–7.1.88).
6. Кабель — медный, исполнение нг(A)-LS (ГОСТ 31565-2012); скрытая прокладка только горизонтально и вертикально, фактические трассы зафиксировать исполнительной схемой до закрытия отделкой.
7. Расчёт нагрузок, токов КЗ, селективности и сечений — по проекту ЭОМ организации с допуском СРО; лист задаёт состав, расположение и группы.
8. Группы без выключателя: L17, L18 — назначить управление до монтажа.
9. Расшифровка клавиш и ведомость изделий — лист 37.

1000 мм · печать 1:1

Изм.	Кол.уч	Лист	№ док.	Подп.	Дата
Разраб.		Кырлан А.С.			21.10.26
Пров.					
ГИП					
Н. контр.					
Утв.					

ГД-2026-010-АИ

Дом 331 м²

Общая площадь 270,67* м² · * размеры приняты, не замерены (реестр — л. 7, К-1)

Дизайн-проект интерьера

Стадия	Лист	Листов
РП	36	159

План выключателей и схема включения · Мансарда

М 1:100

Кырлан Александр Сергеевич

выпуск 18.10.2026 № 9365d64cec · стр. 39 из 197

02

Электрооборудование

Кырлан Александр Сергеевич

выпуск 18.10.2026 № 9365d64cec · стр. 40 из 197

Ведомость электроточек и изделий

Электроточки, изделия, светильники, клавиши выключателей · б/м

Ведомость электроточек

Марка	Пом.	Назначение	Н, мм	Гр.
Р16	1	фартук: мелкая техника	1150	9
Р17**	1	фартук: мелкая техника	1150	9
Р18	1	фартук: мелкая техника	1150	9
Р19	1	фартук: мелкая техника	1150	9
Р20	1	холодильник встроенный М20 (розетка в модуле М21)	150	10
Р21**	1	вытяжка М25 (в модуле, съёмная панель)	2200	10
Р22	1	кухня: мелкая техника	300	10
Р23	1	уборка	300	10
Р24	1	торцевая панель острова М27: мелкая техника	150	10
Р25	1	торцевая панель острова М27: мелкая техника	150	10
Р26	1	посудомоечная машина в острове М27	150	16
ЭВ3	1	варочная панель М22	150	11
ЭВ4**	1	духовой шкаф М22 (вывод в соседнем модуле М23)	150	15
Р9	2	у кровати	600	7
Р10	2	у кровати	600	7
Р11	2	у комода	300	7
Р12**	2	ТВ над комодом (в одной зоне с ТВ2, LAN2)	1100	7
Р13	2	уборка	300	7
Р14	2	уборка у входа	300	7
КУП1**	3	КУП — уравнивание потенциалов (ДСУП)	300	
Р7**	3	стиральная машина, IP44	1000	12
Р8**	3	фен у умывальника, IP44	1000	13
ЭВ4**	3	вентилятор ВР1 (таймер выбега)	2389	3
ЭВ6**	3	полотенцесушитель П10, IP44	700	13
ЭВ9**	4	вывод питания котла и насосов	1200	21
Р1	5	ТВ-зона: телевизор, медиаплеер	950	5
Р2	5	ТВ-зона: саундбар	950	5
Р3	5	торшер у дивана М2	300	5
Р4	5	кресло у окна М4	300	5

Ведомость электроточек (продолжение)

Марка	Пом.	Назначение	Н, мм	Гр.
Р5	5	обеденная зона, буфет М6	300	5
Р6	5	уборка	300	5
Р34	6	уборка	300	6
Р15	8	пылесос, сушилка обуви	300	6
Р16	8	уборка	300	6
Р17**	8	питание слаботочного щита (рядом с ЩС**)	1700	14
ЩК	8	щит квартирный ЩРВ-П-48	1700	
Р36**	10	верстак, электроинструмент	1100	20
Р37**	10	верстак, зарядка аккумуляторов	1100	20
Р38**	10	привод секционных ворот (под потолком у направляющей)	2400	20
Р35	11	балкон: розетка общего назначения, IP44	300	8
Р35	12	балкон: розетка общего назначения, IP44	300	8
Р1	13	у кровати	600	4
Р2	13	у кровати	600	4
Р3	13	рабочий стол	900	4
Р4	13	рабочий стол	900	4
Р5	13	торшер у кресла	300	4
Р6	13	уборка	300	4
КУП1**	15	КУП — уравнивание потенциалов (ДСУП)	300	
Р7**	15	стиральная машина, IP44	1000	12
Р8**	15	фен у умывальника, IP44	1000	13
ЭВ4**	15	вентилятор ВР1 (таймер выбега)	2389	3
ЭВ6**	15	полотенцесушитель П10, IP44	700	13
Р9	16	у кровати	600	17
Р10	16	у кровати	600	17
Р11	16	у комода	300	17
Р12**	16	ТВ над комодом (в одной зоне с ТВ2, LAN2)	1100	17
Р13	16	уборка	300	17
Р14	16	уборка у входа	300	17
Р34	17	уборка	300	6

Ведомость электроточек (продолжение)

Марка	Пом.	Назначение	Н, мм	Гр.
Р9	18	у кровати	600	18
Р10	18	у кровати	600	18
Р11	18	у комода	300	18
Р12**	18	ТВ над комодом (в одной зоне с ТВ2, LAN2)	1100	18
Р13	18	уборка	300	18
Р14	18	уборка у входа	300	18
Р9	19	у кровати	600	19
Р10	19	у кровати	600	19
Р11	19	у комода	300	19
Р12**	19	ТВ над комодом (в одной зоне с ТВ2, LAN2)	1100	19
Р13	19	уборка	300	19
Р14	19	уборка у входа	300	19
КУП2**	20	КУП — уравнивание потенциалов (ДСУП)	300	
Р33**	20	фен у умывальника, IP44	1000	13
ЭВ5**	20	вентилятор ВР3 (таймер выбега)	2389	3
ЭВ7**	20	полотенцесушитель П13, IP44	700	13

Ведомость изделий

Наименование	Марки	Ед.	Кол.
Розетка с з/к и защитными шторками, 16 А	по ведомости точек	шт	62
Розетка IP44 с крышкой, 16 А	Р7**, Р8**, Р33**, Р35	шт	7
Выключатель 1-клав.	S9, S17, S20	шт	3
Выключатель 1-клав. перекрёстный	S8	шт	1
Выключатель 1-клав. проходной	S7, S10, S14, S18, S19	шт	6
Выключатель 2-клав. (перекрёстная + обычная)	S9	шт	1
Выключатель 2-клав. (перекрёстная + проходная)	S1, S5, S16	шт	8
Выключатель 2-клав. перекрёстный	S3, S6, S8, S15	шт	8
Выключатель 2-клав. проходной	S2**, S4, S7	шт	6
Светорегулятор 1-канальный, задний фронт (LED)	S2**	шт	1
Датчик движения ночной подсветки	L11	шт	1

Ведомость изделий (продолжение)

Наименование	Марки	Ед.	Кол.
Рамка 1-постовая	в т. ч. 34 под выключ.	шт	89
Рамка 2-постовая		шт	7
Коробка установочная (подрозетник) Ø68	розетки, выключатели	шт	103
Вывод кабеля под прибор (клеммник)	ЭВ3, ЭВ4**, ЭВ5**, ЭВ6**, ЭВ7**, ЭВ9**	шт	9
Коробка уравнивания потенциалов КУП	КУП1**, КУП2**	шт	3
Блок питания LED 24 В, 30 Вт	БП2	шт	1
Блок питания LED 24 В, 150 Вт, дим.	БП3	шт	1
Блок питания LED 24 В, 200 Вт, дим.	БП4, БП6–БП9	шт	5
Блок питания LED 24 В, 300 Вт, дим.	БП1	шт	1
Блок питания LED 24 В, 20 Вт	БП5	шт	1
Извещатель дымовой автономный	ИП1, ИП2	шт	6
Извещатель тепловой	ИП3, ИП4, ИП6	шт	4
Щит квартирный (состав — лист щита)	ЩК	шт	1
Розетка компьютерная RJ45, кат. 6, с рамкой и подрозетником	LAN1, LAN2, LAN3**	шт	7
Розетка телевизионная (коаксиальная) с рамкой и подрозетником	ТВ1, ТВ2	шт	5
Точка доступа Wi-Fi (оборудование заказчика), питание PoE	AP1**	шт	1
Трубка или монитор домофона (поставка домофонной организации)	ДФ1	шт	1
Щит слаботочный ЩС**: корпус, DIN-рейка, розетки 220 В	ЩС**	шт	1
Патч-панель, портов не менее 8		шт	1
Коммутатор, портов не менее 8, из них PoE 1		шт	1
Кабель домофона — тип по системе поставщика (по лучам от ЩС**, запас 10 %)		м	2,8
Кабель коаксиальный RG-6 (75 Ом) к розеткам ТВ (по лучам от ЩС**, запас 10 %)		м	70,6
Кабель U/UTP кат. 5e (LAN, Wi-Fi и камеры по PoE) (по лучам от ЩС**, запас 10 %)		м	11,9
Кабель U/UTP кат. 6 (LAN, Wi-Fi и камеры по PoE) (по лучам от ЩС**, запас 10 %)		м	96,4

Примечания

1. Ведомости сведены с планов розеток, освещения и выключателей; марки, группы и высоты — те же, что у знаков на планах.
2. Механизмы, рамки и светорегуляторы — одной серии; число постов и клавиш сверено с выбранной серией. Перекрёстная клавиша — отдельный механизм серии.
3. За отметку 0,000 принят уровень чистого пола. Высоты Н — от чистого пола до оси изделия; привязки — от чистовой грани стены до оси механизма (у рамки на несколько постов — до оси рамки).
4. Розеточные и мокрые линии — через УЗО или дифавтомат с током утечки не более 30 мА (ПУЭ 7.1.79); в санузле выполнить ДСУП (ПУЭ 7.1.87–7.1.88).
5. Кабель — медный, исполнение нг(A)-LS (ГОСТ 31565-2012); скрытая прокладка только горизонтально и вертикально, фактические трассы зафиксировать исполнительной схемой до закрытия отделкой.
6. Расчёт нагрузок, токов КЗ, селективности и сечений — по проекту ЭОМ организации с допуском СРО; лист задаёт состав, расположение и группы.
7. Ведомости занимают 2 листов этого наименования: таблицы, не вошедшие в поле листа, продолжены на следующем листе.

Допущения и предложения на листе. Знак «**» предложено (согласовать). См. лист открытых вопросов (лист 7).

Изм.	Кол.уч	Лист	№ док.	Подп.	Дата
Разраб.		Кырлан А.С.			21.10.26
Пров.					
ГИП					
Н. контр.					
Утв.					

ГД-2026-010-АИ

Дом 331 м²

Общая площадь 270,67* м² · * размеры приняты, не замерены (реестр — л. 7, К-1)

Дизайн-проект интерьера

Стадия	Лист	Листов
РП	37	159

Ведомость электроточек и изделий

М б/м

Кырлан Александр Сергеевич

Ведомость электроточек и изделий (продолжение)

Электроточки, изделия, светильники, клавиши выключателей · б/м

Ведомость светильников

Поз.	Марки	Тип	Кол.	P, Вт	Ф, лм	IP	Тц/Ra
1	Св1–Св8, Св31–Св37	встраиваемый точечный	15	12	1000		3000/90
2	Св38, Св39	линейный светильник	2	8	700		3000/90
3	Св40	светодиодная лента, 10,2 м	1	97,9	9180		2700/90
4	Св17–Св22	встраиваемый точечный	24	12	1050		2700/90
5	Св23	светодиодная лента, 5,4 м	1	51,8	4860		2700/90
6	Св10, Св11, Св24, Св25	настенный (бра), H=1500	10	6	400		2700/90
7	Св12–Св14, Св51	встраиваемый точечный	7	6	500	44	3000/90
8	Св15, Св52	настенный (бра), H=1900	3	8	600	44	3000/90
9	Св16, Св55, Св58	потолочный накладной	4	10	900		3000/90
10	Св9	подвесной	1	15	1200		2700/90
11	Св10	светодиодная лента, 21,1 м	1	202,6	18990		2700/90
12	Св26–Св29, Св53, Св54	встраиваемый точечный	8	7	600		3000/90
13	Св30	светодиодная лента, 1,8 м	1	8,6	270		2700/90
14	Св56, Св57	потолочный накладной	2	24	2500		3000/90
15	Св54	встраиваемый точечный	2	9	800	44	3000/90
16	Св1–Св8	встраиваемый точечный	8	12	1000		2700/90
17	Св9, Св23	светодиодная лента, 6 м	2	57,6	5400		2700/90
18	Св23	светодиодная лента, 3,2 м	1	30,7	2880		2700/90
19	Св23	светодиодная лента, 15,5 м	1	148,8	13950		2700/90
20	Св50	встраиваемый точечный	1	7	600	44	3000/90

Расшифровка клавиш

Марка	Пом.	H, мм	Клав.	Механизм	Группа: светильники
S1	5	900	1	перекрёстный	L1: Св1–Св8
			2	проходной	L2: Св9

Расшифровка клавиш (продолжение)

Марка	Пом.	H, мм	Клав.	Механизм	Группа: светильники
S1	13	900	1	перекрёстный	L1: Св1–Св8
			2	проходной	L2: Св9
S2**	5	900	1	светорегулятор	L3: Св10, Св11
S2**	13	800	1	проходной	L1: Св1–Св8
			2	проходной	L3: Св10, Св11
S3	13	800	1	перекрёстный	L1: Св1–Св8
			2	перекрёстный	L3: Св10, Св11
S4	2	900	1	проходной	L7: Св17–Св22
			2	проходной	L8: Св23
S4	16	900	1	проходной	L7: Св17–Св22
			2	проходной	L8: Св23
S4	18	900	1	проходной	L7: Св17–Св22
			2	проходной	L8: Св23
S4	19	900	1	проходной	L7: Св17–Св22
			2	проходной	L8: Св23
S5	2	800	1	перекрёстный	L7: Св17–Св22
			2	проходной	L9: Св24, Св25
S5	16	800	1	перекрёстный	L7: Св17–Св22
			2	проходной	L9: Св24, Св25
S5	18	800	1	перекрёстный	L7: Св17–Св22
			2	проходной	L9: Св24, Св25
S5	19	800	1	перекрёстный	L7: Св17–Св22
			2	проходной	L9: Св24, Св25
S6	2	800	1	перекрёстный	L7: Св17–Св22
			2	перекрёстный	L9: Св24, Св25
S6	16	800	1	перекрёстный	L7: Св17–Св22
			2	перекрёстный	L9: Св24, Св25
S6	18	800	1	перекрёстный	L7: Св17–Св22
			2	перекрёстный	L9: Св24, Св25
S6	19	800	1	перекрёстный	L7: Св17–Св22
			2	перекрёстный	L9: Св24, Св25
S7	1	900	1	проходной	L4: Св12–Св14, Св31–Св37
			2	проходной	L5: Св15, Св38, Св39

Расшифровка клавиш (продолжение)

Марка	Пом.	H, мм	Клав.	Механизм	Группа: светильники
S7	8	900	1	проходной	L10: Св26–Св29, Св53, Св54
S8	1	900	1	перекрёстный	L4: Св12–Св14, Св31–Св37
			2	перекрёстный	L5: Св15, Св38, Св39
S8	8	900	1	перекрёстный	L10: Св26–Св29, Св53, Св54
S9	1	900	1	обычный	L17: Св50, Св51, Св54
S9	8	900	1	перекрёстный	L10: Св26–Св29, Св53, Св54
			2	обычный	L11: Св30
S10	1	900	1	проходной	L6: Св16, Св40
S14	6	900	1	проходной	L10: Св26–Св29, Св53, Св54
S14	17	900	1	проходной	L10: Св26–Св29, Св53, Св54
S15	6	900	1	перекрёстный	L4: Св12–Св14, Св31–Св37
			2	перекрёстный	L5: Св15, Св38, Св39
S15	17	900	1	перекрёстный	L4: Св12–Св14, Св31–Св37
			2	перекрёстный	L5: Св15, Св38, Св39
S16	6	900	1	проходной	L6: Св16, Св40
			2	перекрёстный	L10: Св26–Св29, Св53, Св54
S16	17	900	1	проходной	L6: Св16, Св40
			2	перекрёстный	L10: Св26–Св29, Св53, Св54
S17	9	900	1	обычный	L19: Св55
S18	10	900	1	проходной	L20: Св56, Св57
S19	10	900	1	проходной	L20: Св56, Св57
S20	4	900	1	обычный	L21: Св58

Допущения и предложения на листе

Основа листа: размеры и контуры этажей подобраны проектировщиком по составу помещений и площадям этажей с картинки 470 px (размеры на ней не читаются); обмер и исходный проект — задание (К-1); высоты: 1-й этаж 2800 мм, мансарда 2700 мм (горизонтальная часть) приняты; скаты кровли мансарды приняты по картинке: колено 1200 мм, уклон 45°, конёк вдоль длинной стороны; проект КР — задание (К-2); наружные стены 400 мм, перегородки 120 мм приняты (К-1); разрешённая мощность 15 кВт принята по типовым ТУ для частного дома (К-4); подрайон климата не задан — принят не северный (жилые от 2,5 м) (К-7).

Знак «**» — предложение проектировщика, заказчиком не утверждено (согласовать с заказчиком): записи в реестре нет: S2 — светорегулятор добавлен под диммируемую ленту L3; уровни сценариев выбраны конвейером.

См. лист открытых вопросов (лист 7, записи К-1, К-2, К-4, К-7).

Примечания

1. Продолжение ведомостей: лист 2 из 2 этого наименования; таблицы, прерванные на предыдущем листе, продолжены с заголовком «(продолжение)».
2. За отметку 0,000 принят уровень чистого пола. Высоты H — от чистого пола до оси изделия; привязки — от чистовой грани стены до оси механизма (у рамки на несколько постов — до оси рамки).
3. Розеточные и мокрые линии — через УЗО или дифавтомат с током утечки не более 30 мА (ПУЭ 7.1.79); в санузле выполнить ДСУП (ПУЭ 7.1.87–7.1.88).
4. Кабель — медный, исполнение нг(A)-LS (ГОСТ 31565-2012); скрытая прокладка только горизонтально и вертикально, фактические трассы зафиксировать исполнительной схемой до закрытия отделкой.
5. Расчёт нагрузок, токов КЗ, селективности и сечений — по проекту ЭОМ организации с допуском СРО; лист задаёт состав, расположение и группы.

Изм.	Кол.уч	Лист	№ док.	Подп.	Дата
Разраб.		Кырлан А.С.			21.10.26
Пров.					
ГИП					
Н. контр.					
Утв.					

ГД-2026-010-АИ

Дом 331 м²

Общая площадь 270,67* м² · * размеры приняты, не замерены (реестр — л. 7, К-1)

Дизайн-проект интерьера

Стадия	Лист	Листов
РП	38	159

Ведомость электроточек и изделий (продолжение)

М б/м

Кырлан Александр Сергеевич

выпуск 18.10.2026 № 9365d64cec · стр. 42 из 197

Однолинейная схема щита

Щит квартирный ЩК · гр. 1—11 из 21 · без масштаба

ПРЕДВАРИТЕЛЬНО · не для производства работ · открыто пунктов: 6 (реестр — л. 7)

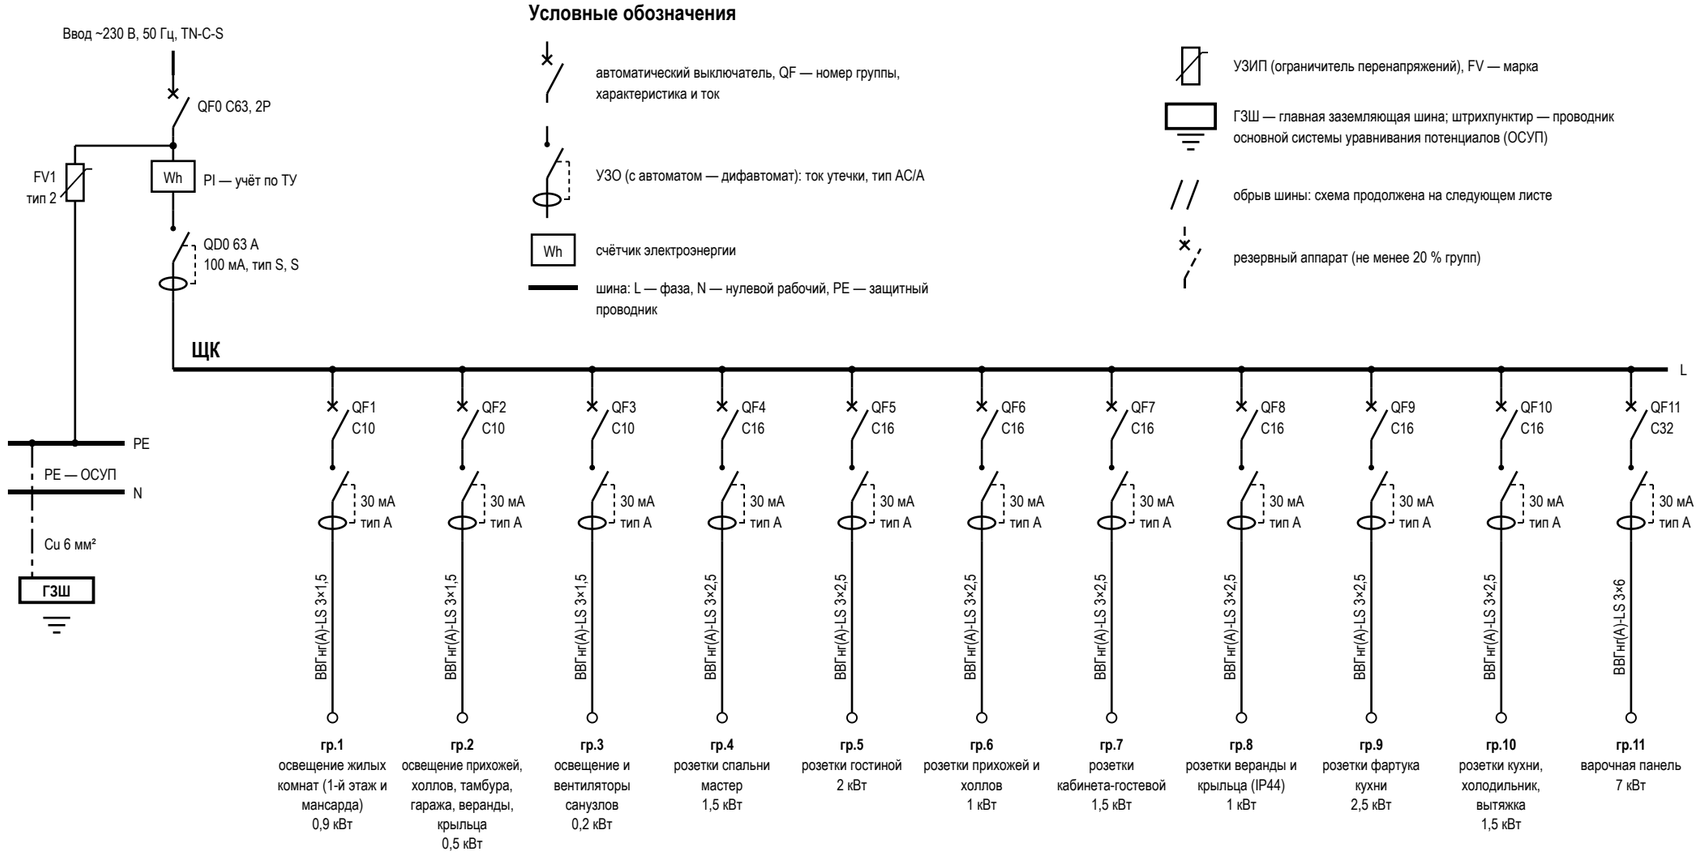

Условные обозначения

- автоматический выключатель, QF — номер группы, характеристика и ток
- УЗО (с автоматом — дифавтомат): ток утечки, тип AC/A
- Wh — счётчик электроэнергии
- шина: L — фаза, N — нулевой рабочий, PE — защитный проводник
- УЗИП (ограничитель перенапряжений), FV — марка
- ГЗШ — главная заземляющая шина; штрихпунктир — проводник основной системы уравнивания потенциалов (ОСУП)
- обрыв шины: схема продолжена на следующем листе
- резервный аппарат (не менее 20 % групп)

Данные щитка

Показатель	Значение
Номер щитка	ЩК
Тип	ЩРВ-П-72, IP41
Уст. мощность, кВт	36,1
Разреш. мощность, кВт	15
Расчётная, кВт	13,8
Автоматы 1п: занят. / рез.	21 / 5
Модулей: всего / занято	72 / 48
Ток на вводе, А	63
Вводной аппарат	QF0 C63, 2P
УЗИП	FV1, тип 2, ЩК, после счётчика
ГЗШ, проводник ОСУП	Cu 6 мм²
Листов схемы	2 (группы по листам)

Таблица групп щита ЩК и кабельный журнал

№	Назначение	Помещения	Автомат	УЗО / дифавтомат	Кабель	Длина, м	Р, кВт	Точек
1	освещение жилых комнат (1-й этаж и мансарда)	1, 2, 5, 6, 7, 13, 14, 16, 17, 18, 19	C10	30 мА, тип A	ВВГнг(A)-LS 3×1,5	95	0,9	99
2	освещение прихожей, холлов, тамбура, гаража, веранды, крыльца	1, 4, 6, 8, 9, 10, 11, 12, 17	C10	30 мА, тип A	ВВГнг(A)-LS 3×1,5	80	0,5	26
3	освещение и вентиляторы санузлов	3, 6, 15, 17, 20	C10	30 мА, тип A	ВВГнг(A)-LS 3×1,5	45	0,2	16
4	розетки спальни мастер	13	C16	30 мА, тип A	ВВГнг(A)-LS 3×2,5	30	1,5	6
5	розетки гостиной	5	C16	30 мА, тип A	ВВГнг(A)-LS 3×2,5	30	2	6
6	розетки прихожей и холлов	6, 8, 17	C16	30 мА, тип A	ВВГнг(A)-LS 3×2,5	40	1	4
7	розетки кабинета-гостевой	2	C16	30 мА, тип A	ВВГнг(A)-LS 3×2,5	20	1,5	6
8	розетки веранды и крыльца (IP44)	11, 12	C16	30 мА, тип A	ВВГнг(A)-LS 3×2,5	25	1	2
9	розетки фартука кухни	1	C16	30 мА, тип A	ВВГнг(A)-LS 3×2,5	15	2,5	4
10	розетки кухни, холодильник, вытяжка	1	C16	30 мА, тип A	ВВГнг(A)-LS 3×2,5	18	1,5	6
11	варочная панель	1	C32	30 мА, тип A	ВВГнг(A)-LS 3×6	15	7	1

Допущения и предложения на листе

Основа листа: размеры и контуры этажей подобраны проектировщиком по составу помещений и площадям этажей с картинки 470 px (размеры на ней не читаются); обмер и исходный проект — задание (К-1); высоты: 1-й этаж 2800 мм, мансарда 2700 мм (горизонтальная часть) приняты; скаты кровли мансарды приняты по картинке: колено 1200 мм, уклон 45°, конёк вдоль длинной стороны; проект КР — задание (К-2); наружные стены 400 мм, перегородки 120 мм приняты (К-1); разрешённая мощность 15 кВт принята по типовым ТУ для частного дома (К-4); подрайон климата не задан — принят не северный (жилые от 2,5 м) (К-7).

Открытые вопросы и конфликты по листу: К-4.

См. лист открытых вопросов (лист 7, записи К-1, К-2, К-4, К-7).

Примечания

1. Схема однолинейная: одна линия — фаза, N и PE группы; аппараты — в отключённом положении (ГОСТ 2.702, ГОСТ 2.755). Номера групп — как у точек на планах (гр.). За отметку 0,000 принят уровень чистого пола; высота щита — по плану розеток.
2. Розеточные и мокрые линии — через УЗО или дифавтомат с током утечки не более 30 мА (ПУЭ 7.1.79); в санузле выполнить ДСУП (ПУЭ 7.1.87–7.1.88).
3. УЗО тип A — для линий с электроникой, стиральной и посудомоечной машиной, LED-драйверами; тип AC — только для чисто активной нагрузки.
4. Кабель — медный, исполнение нг(A)-LS (ГОСТ 31565-2012); скрытая прокладка только горизонтально и вертикально, фактические трассы зафиксировать исполнительной схемой до закрытия отделкой.
5. Номинал автомата — не выше допустимого тока кабеля: 1,5 мм² — до 10 А, 2,5 мм² — до 16 А. Резерв щита — не менее 20 % модулей.
6. Расчёт нагрузок, токов КЗ, селективности и сечений — по проекту ЭОМ организации с допуском СРО; лист задаёт состав, расположение и группы.
7. УЗИП FV1 — после вводного автомата, проводник к шине PE — кратчайший, без петель. Шина PE щита соединяется с ГЗШ проводником ОСУП; к ГЗШ присоединяются трубы водопровода и отопления на вводе в квартиру (ПУЭ 7.1.87). Шины N и PE — раздельные, после разделения PEN не объединяются.
8. До подключения нагрузки — приёмо-сдаточные испытания с протоколом: сопротивление изоляции линий не менее 0,5 МОм, срабатывание УЗО по току и времени, непрерывность защитных проводников PE (ПУЭ, гл. 1.8).

Изм.	Кол.уч	Лист	№ док.	Подп.	Дата
Разраб.		Кырлан А.С.			21.10.26
Пров.					
ГИП					
Н. контр.					
Утв.					

ГД-2026-010-АИ

Дом 331 м²

Общая площадь 270,67* м² · * размеры приняты, не замерены (реестр — л. 7, К-1)

Дизайн-проект интерьера

Стадия	Лист	Листов
РП	39	159

Однолинейная схема щита

М б/м

Кырлан Александр Сергеевич

выпуск 18.10.2026 № 9365d64cec · стр. 43 из 197

Однолинейная схема щита (продолжение)

Щит квартирный ЩК · гр. 12—21 из 21 · без масштаба

Продолжение однолинейной схемы щита ЩК, начало — лист 39

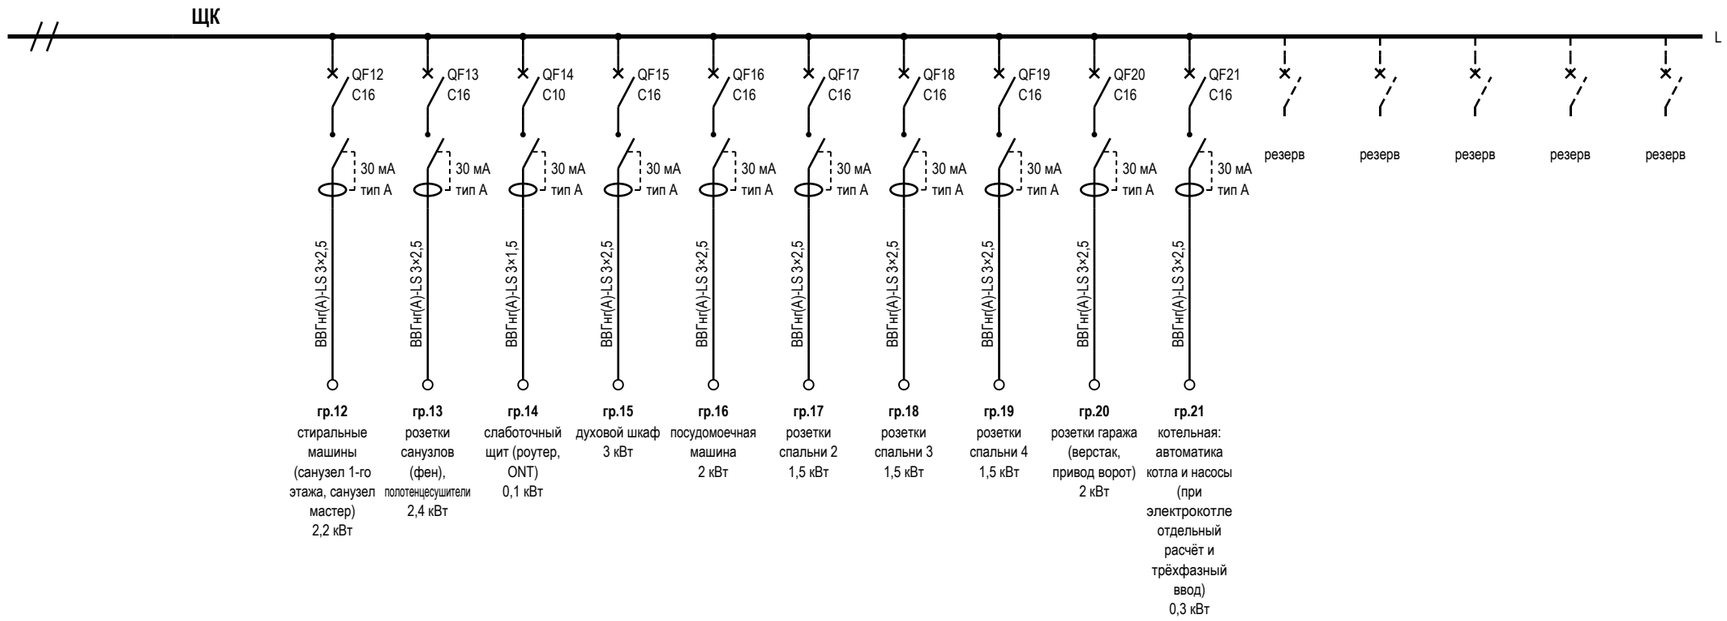

Таблица групп щита ЩК и кабельный журнал (продолжение)

№	Назначение	Помещения	Автомат	УЗО / дифавтомат	Кабель	Длина, м	Р, кВт	Точек
12	стиральные машины (санузел 1-го этажа, санузел мастер)	3, 15	C16	30 мА, тип A	ВВГнг(A)-LS 3×2,5	30	2,2	2
13	розетки санузлов (фен), полотенцесушители	3, 15, 20	C16	30 мА, тип A	ВВГнг(A)-LS 3×2,5	45	2,4	6
14	слаботочный щит (роутер, ONT)	8	C10	30 мА, тип A	ВВГнг(A)-LS 3×1,5	5	0,1	1
15	духовой шкаф	1	C16	30 мА, тип A	ВВГнг(A)-LS 3×2,5	15	3	1
16	посудомоечная машина	1	C16	30 мА, тип A	ВВГнг(A)-LS 3×2,5	15	2	1
17	розетки спальни 2	16	C16	30 мА, тип A	ВВГнг(A)-LS 3×2,5	30	1,5	6
18	розетки спальни 3	18	C16	30 мА, тип A	ВВГнг(A)-LS 3×2,5	35	1,5	6
19	розетки спальни 4	19	C16	30 мА, тип A	ВВГнг(A)-LS 3×2,5	35	1,5	6
20	розетки гаража (верстак, привод ворот)	10	C16	30 мА, тип A	ВВГнг(A)-LS 3×2,5	30	2	3
21	котельная: автоматика котла и насосы (при электрокотле отдельный расчёт и трёхфазный ввод)	4	C16	30 мА, тип A	ВВГнг(A)-LS 3×2,5	10	0,3	1
	Итого по сечениям ВВГнг(A)-LS (все группы щита), м: 3×1,5 — 225; 3×2,5 — 423; 3×6 — 15					663		

Примечания

1. Лист — продолжение однолинейной схемы щита ЩК: начало, данные щитка и условные обозначения — лист 39. Ввод, учёт, вводной аппарат, УЗИП, шины N и PE и ГЗШ показаны там же; шина L листа — та же шина щита.
2. Схема однолинейная: одна линия — фаза, N и PE группы; аппараты — в отключённом положении (ГОСТ 2.702, ГОСТ 2.755). Номера групп — как у точек на планах (гр.). За отметку 0,000 принят уровень чистого пола; высота щита — по плану розеток.
3. Розеточные и мокрые линии — через УЗО или дифавтомат с током утечки не более 30 мА (ПУЭ 7.1.79); в санузле выполнить ДСУП (ПУЭ 7.1.87–7.1.88).
4. УЗО тип A — для линий с электроникой, стиральной и посудомоечной машиной, LED-драйверами; тип AC — только для чисто активной нагрузки.
5. Кабель — медный, исполнение нг(A)-LS (ГОСТ 31565-2012); скрытая прокладка только горизонтально и вертикально, фактические трассы зафиксировать исполнительной схемой до закрытия отделкой.
6. Номинал автомата — не выше допустимого тока кабеля: 1,5 мм² — до 10 А, 2,5 мм² — до 16 А. Резерв щита — не менее 20 % модулей.
7. Расчёт нагрузок, токов КЗ, селективности и сечений — по проекту ЭОМ организации с допуском СРО; лист задаёт состав, расположение и группы.
8. До подключения нагрузки — приёмо-сдаточные испытания с протоколом: сопротивление изоляции линий не менее 0,5 МОм, срабатывание УЗО по току и времени, непрерывность защитных проводников PE (ПУЭ, гл. 1.8).

Допущения и предложения на листе

Основа листа: размеры и контуры этажей подобраны проектировщиком по составу помещений и площадям этажей с картинки 470 px (размеры на ней не читаются); обмер и исходный проект — задание (К-1); высоты: 1-й этаж 2800 мм, мансарда 2700 мм (горизонтальная часть) приняты; скаты кровли мансарды приняты по картинке: колено 1200 мм, уклон 45°, конёк вдоль длинной стороны; проект КР — задание (К-2); наружные стены 400 мм, перегородки 120 мм приняты (К-1); разрешённая мощность 15 кВт принята по типовым ТУ для частного дома (К-4); подрайон климата не задан — принят не северный (жилые от 2,5 м) (К-7).
См. лист открытых вопросов (лист 7, записи К-1, К-2, К-4, К-7).

Изм.	Кол.уч	Лист	№ док.	Подп.	Дата
Разраб.		Кырлан А.С.			21.10.26
Пров.					
ГИП					
Н. контр.					
Утв.					

ГД-2026-010-АИ

Дом 331 м²

Общая площадь 270,67* м² · * размеры приняты, не замерены (реестр — л. 7, К-1)

Дизайн-проект интерьера

Стадия	Лист	Листов
РП	40	159

Однолинейная схема щита (продолжение)

М б/м

Кырлан Александр Сергеевич

выпуск 18.10.2026 № 9365d64cec · стр. 44 из 197

План принципиальных трасс · 1-й этаж

Силовые трассы и объёмы электромонтажа, слаботочка в объёмах · размеры в мм

ПРЕДВАРИТЕЛЬНО · не для производства работ · открыто пунктов: 6 (реестр — л. 7)

Допущения и предложения на листе

Основа листа: размеры и контуры этажей подобраны проектировщиком по составу помещений и площадям этажей с картинки 470 px (размеры на ней не читаются); обмер и исходный проект — задание (К-1); высоты: 1-й этаж 2800 мм, мансарда 2700 мм (горизонтальная часть) приняты; скаты кровли мансарды приняты по картинке: колено 1200 мм, уклон 45°, конёк вдоль длинной стороны; проект КР — задание (К-2); наружные стены 400 мм, перегородки 120 мм приняты (К-1); разрешённая мощность 15 кВт принята по типовым ТУ для частного дома (К-4); подрайон климата не задан — принят не северный (жилые от 2,5 м) (К-7).

Знак «**» — предложение проектировщика, заказчиком не утверждено (согласовать с заказчиком): записи в реестре нет: ЩС — щит слаботочный: место и состав.

См. лист открытых вопросов (лист 7, записи К-1, К-2, К-4, К-7).

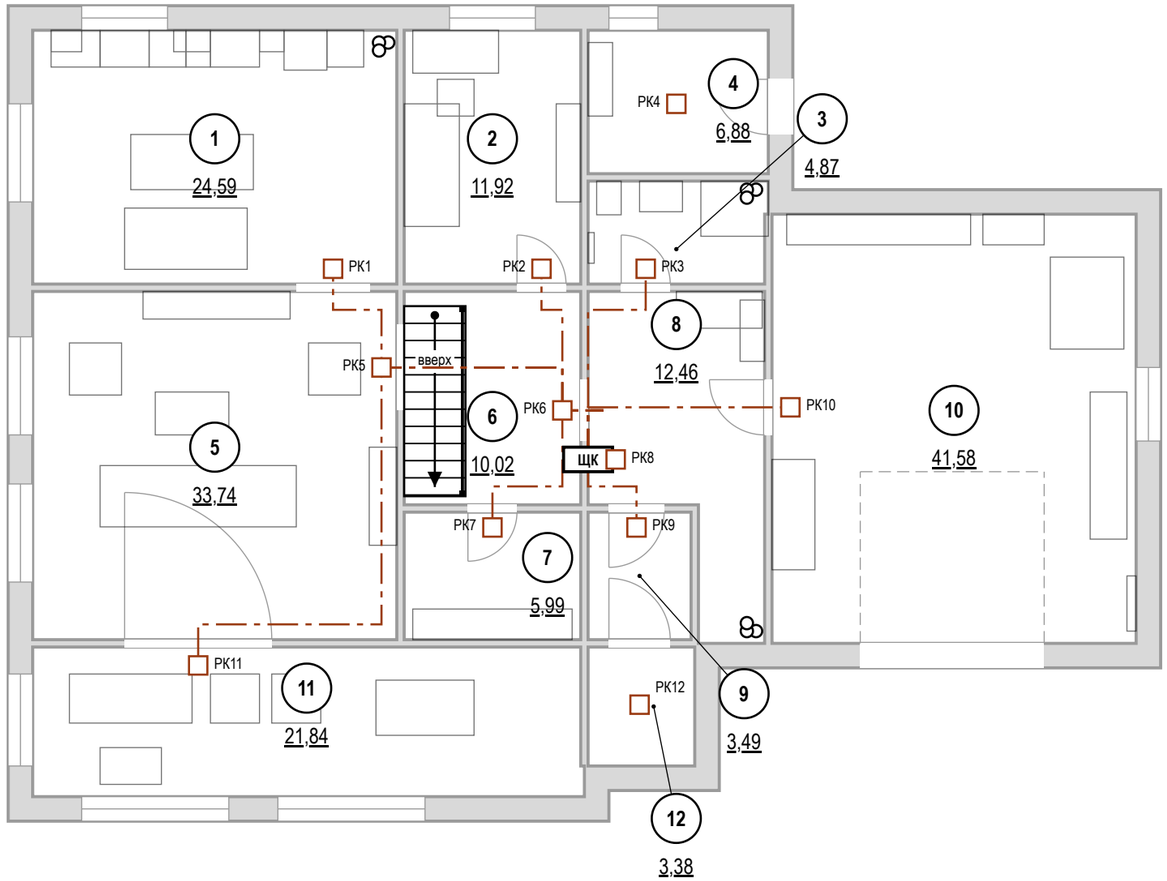

Кабель по группам ВВГнг(А)-LS, м

Гр.	мм²	Трасса	Данные
1	3×1,5	141,2	95
2	3×1,5	136,2	80
3	3×1,5	25,8	45
5	3×2,5	33,5	30
6	3×2,5	13,3	40
7	3×2,5	24,9	20
8	3×2,5	35	25
9	3×2,5	32,1	15
10	3×2,5	33,6	18

Гр.	мм²	Трасса	Данные
11	3×6	23,6	15
12	3×2,5	12,3	30
13	3×2,5	14	45
14	3×1,5	3,8	5
15	3×2,5	22,7	15
16	3×2,5	16,2	15
20	3×2,5	23,9	30
21	3×2,5	16,2	10
Σ		**608,3**	**663**

Экспликация помещений

№	Помещение	Площадь, м²
1	Кухня-столовая	24,59
2	Кабинет-гостевая	11,92
3	Санузел 1 этажа	4,87
4	Котельная	6,88
5	Гостиная	33,74
6	Холл с лестницей	10,02
7	Кладовая	5,99
8	Прихожая	12,46
9	Тамбур	3,49
10	Гараж	41,58
11	Веранда *	21,84
12	Крыльцо *	3,38
	Итого (общая площадь)	270,67

Объёмы прокладки

Работа, материал	Ед.	Кол.
Гофротруба Ø20 в потолочном пространстве	м	272,4
Кабель-канал плинтуса для силовых линий	м	156,7
Короб или накладной канал для вертикальных спусков и подъёмов	м	93
Коробка распределительная (РК) над дверью помещения	шт	12
Слаботочка: кабель домофона	м	2,8
Слаботочка: Кабель коаксиальный RG-6 (75 Ом) к розеткам ТВ	м	30
Слаботочка: Кабель U/UTP кат. 5е (LAN, Wi-Fi и камеры по PoE)	м	11,9
Слаботочка: U/UTP кат. 6 (LAN, Wi-Fi, камеры)	м	33,4
Слаботочка: гофротруба Ø20 отдельно от силовых	м	70,3

Штробы — только после заключения

Работа	Ед.	Кол.
Вертикальные штробы 20×20 мм от потолка до каждой настенной точки (в маршрут без штроб не входят)	м	110,98

Условные обозначения

- **ЩК** — щит квартирный
- РК — распределительная коробка над дверью помещения
- магистраль от щита к РК: потолочное пространство, гофра
- мебель и сантехприборы — подложка

Примечания

1. За отметку 0,000 принят уровень чистого пола. Высоты Н — от чистого пола до оси изделия; привязки — от чистовой грани стены до оси механизма (у рамки на несколько постов — до оси рамки).
2. Розеточные и мокрые линии — через УЗО или дифавтомат с током утечки не более 30 мА (ПУЭ 7.1.79); в санузле выполнить ДСУП (ПУЭ 7.1.87–7.1.88).
3. Кабель — медный, исполнение нг(А)-LS (ГОСТ 31565-2012); скрытая прокладка только горизонтально и вертикально, фактические трассы зафиксировать исполнительной схемой до закрытия отделкой.
4. Расчёт нагрузок, токов КЗ, селективности и сечений — по проекту ЭОМ организации с допуском СРО; лист задаёт состав, расположение и группы.
5. Длины — по плану: от щита вверх в потолочное пространство, по дверям и коридору без захода в мокрые помещения к распределительной коробке над дверью, далее к точкам; вертикали считаются вниз и обратно (у последней точки цепочки — в один конец); запас 10 %. Трассы принципиальные: фактическую зафиксировать исполнительной схемой до закрытия отделкой.
6. Несущие стены не определены: штробы в стенах не выполнять. Маршрут проложен без штроб: горизонтали — за потолком в гофре (272,4 м) и в кабель-канале плинтуса (156,7 м), вертикали — в коробе или накладном канале (163,7 м кабеля). Точек: за потолком — 47, спуск из потолка — 9, по плинтусу — 20, плинтус и подъём 34.
7. Вариант со штробами — работа после технического заключения: 110,98 м вертикальных штроб от потолка до каждой настенной точки; условие — только после технического заключения: стена не несущая (или вертикальная штроба в несущей согласована конструктором), глубина и ширина 20–25 мм, не в зонах 0–2 ванной. Без заключения и согласования конструктора в смету и в график эта работа не входит.
8. В данных проекта (журнал щита) длины кабеля внесены оценкой (663 м), по трассам из геометрии — 608 м (-8 %): к закупке и в смету принимать длины по трассам, а оценку в данных проекта заменить.
9. Слаботочные сети: кабели и точки считаются по лучам от ЩС** (лист слаботочных сетей): 78 м, портов патч-панели и коммутатора не менее 4; из точек 2 предложения листа слаботочки, не подтверждённые заказчиком. Изделия — в ведомости изделий.

1000 мм · печать 1:1

Изм.	Кол.уч	Лист	№ док.	Подп.	Дата
Разраб.		Кырлан А.С.			21.10.26
Пров.					
ГИП					
Н. контр.					
Утв.					

ГД-2026-010-АИ

Дом 331 м²

Общая площадь 270,67* м² · * размеры приняты, не замерены (реестр — л. 7, К-1)

Дизайн-проект интерьера

Стадия	Лист	Листов
РП	41	159

План принципиальных трасс · 1-й этаж

М 1:100

Кырлан Александр Сергеевич

выпуск 18.10.2026 № 9365d64cec · стр. 45 из 197

План принципиальных трасс · Мансарда

Силовые трассы и объёмы электромонтажа, слаботочка в объёмах · размеры в мм

ПРЕДВАРИТЕЛЬНО · не для производства работ · открыто пунктов: 6 (реестр — л. 7)

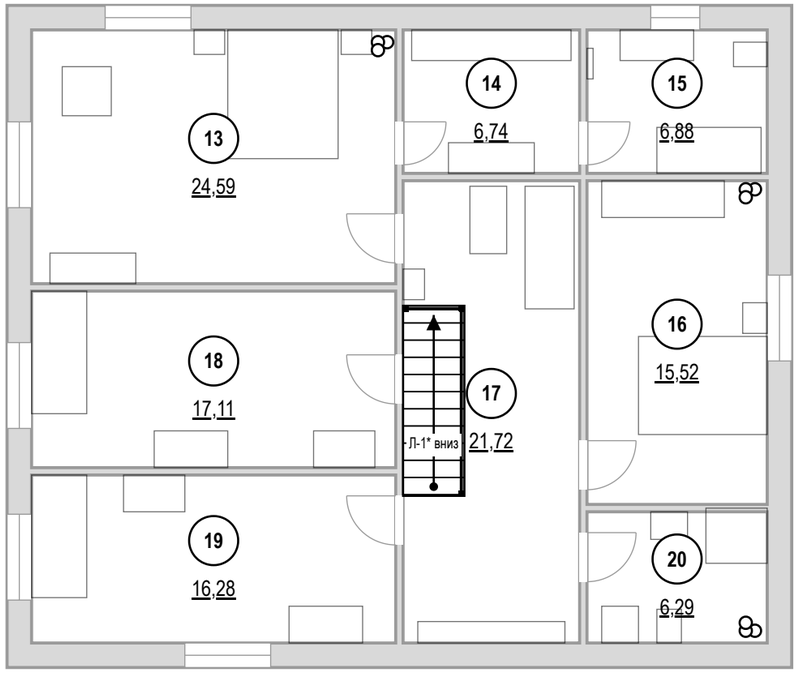

Трассы не построены

нет точки щита квартирного (points kind: panel) — трассу строить не от чего

Экспликация помещений

№	Помещение	Площадь, м²
13	Спальня мастер	24,59
14	Гардеробная мастер	6,74
15	Санузел мастер	6,88
16	Спальня 2	15,52
17	Холл мансарды	21,72
18	Спальня 3	17,11
19	Спальня 4	16,28
20	Санузел 2	6,29
	Итого (общая площадь)	270,67

Условные обозначения

- ЩК — щит квартирный
- РК — распределительная коробка над дверью помещения
- магистраль от щита к РК: потолочное пространство, гофра
- мебель и сантехприборы — подложка

Допущения и предложения на листе

Основа листа: размеры и контуры этажей подобраны проектировщиком по составу помещений и площадям этажей с картинки 470 px (размеры на ней не читаются); обмер и исходный проект — задание (К-1); высоты: 1-й этаж 2800 мм, мансарда 2700 мм (горизонтальная часть) приняты; скаты кровли мансарды приняты по картинке: колено 1200 мм, уклон 45°, конёк вдоль длинной стороны; проект КР — задание (К-2); наружные стены 400 мм, перегородки 120 мм приняты (К-1); разрешённая мощность 15 кВт принята по типовым ТУ для частного дома (К-4); подрайон климата не задан — принят не северный (жилые от 2,5 м) (К-7).

Знак «*» — принято, не замерено и не подтверждено (замерить на объекте): К-6: Л-1 — габарит марша снят с картинки заказчика (11 проступей в холле 3,6 м), а до отм. +3,150 нужно 18 подъёмов — одномаршевая не встаёт: решение по К-6.

См. лист открытых вопросов (лист 7, записи К-1, К-2, К-4, К-6, К-7).

Примечания

1. За отметку 0,000 принят уровень чистого пола. Высоты Н — от чистого пола до оси изделия; привязки — от чистовой грани стены до оси механизма (у рамки на несколько постов — до оси рамки).
2. Розеточные и мокрые линии — через УЗО или дифавтомат с током утечки не более 30 мА (ПУЭ 7.1.79); в санузле выполнить ДСУП (ПУЭ 7.1.87–7.1.88).
3. Кабель — медный, исполнение нг(А)-LS (ГОСТ 31565-2012); скрытая прокладка только горизонтально и вертикально, фактические трассы зафиксировать исполнительной схемой до закрытия отделкой.
4. Расчёт нагрузок, токов КЗ, селективности и сечений — по проекту ЭОМ организации с допуском СРО; лист задаёт состав, расположение и группы.
5. Щит квартиры (дома) — на 1-м этаже: кабели групп Мансарда поднимаются от щита в вертикальном кабель-канале (коробе) у лестницы и далее за потолком к точкам. Место короба и проход через перекрытие — задание конструктору; длины трасс этажа считаются после этого решения.

1000 мм · печать 1:1

Изм.	Кол.уч	Лист	№ док.	Подп.	Дата
Разраб.		Кырлан А.С.			21.10.26
Пров.					
ГИП					
Н. контр.					
Утв.					

ГД-2026-010-АИ

Дом 331 м²

Общая площадь 270,67* м² · * размеры приняты, не замерены (реестр — л. 7, К-1)

Дизайн-проект интерьера

Стадия	Лист	Листов
РП	42	159

План принципиальных трасс · Мансарда

М 1:100

Кырлан Александр Сергеевич

План слаботочных сетей · 1-й этаж

Интернет, ТВ, домофон · размеры в мм · высоты от чистого пола

ПРЕДВАРИТЕЛЬНО · не для производства работ · открыто пунктов: 6 (реестр — л. 7)

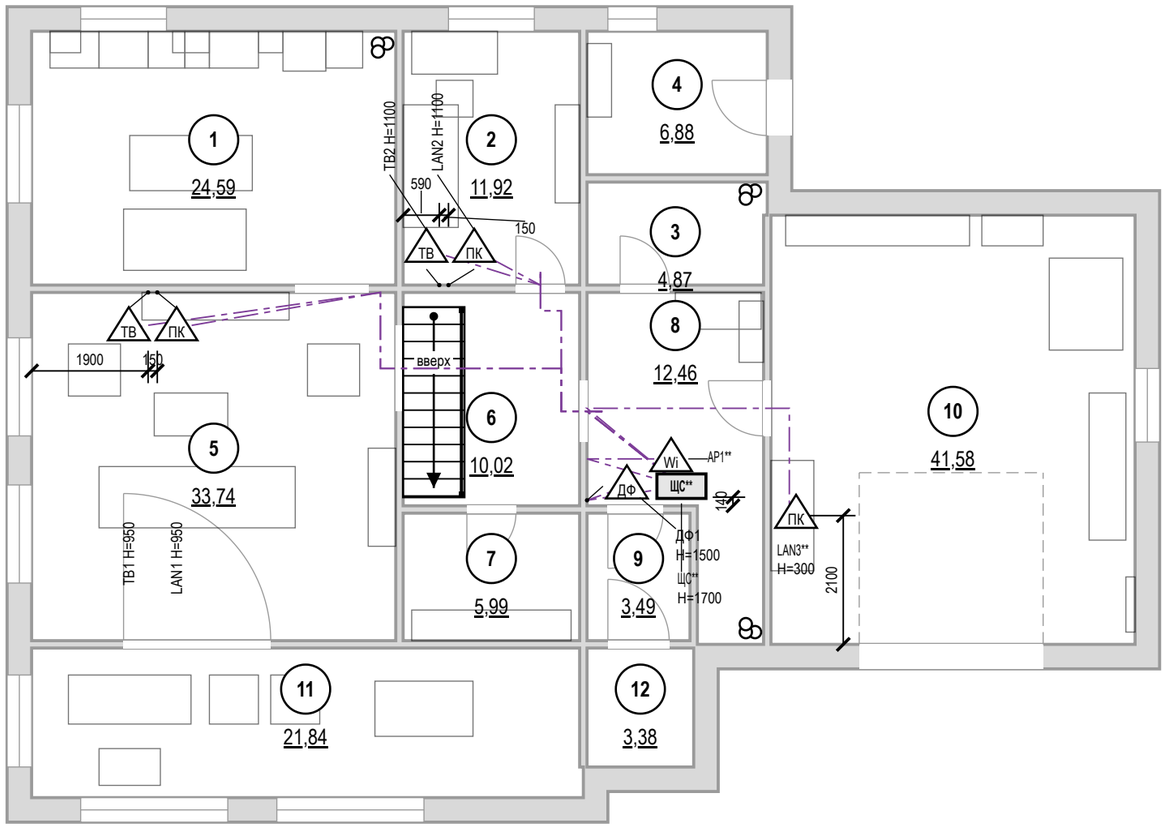

Ведомость слаботочных точек

Марка	Пом.	Назначение	H, мм	Кабель
TB2	2	розетка ТВ	1100	RG-6
LAN2	2	розетка LAN (RJ45)	1100	U/UTP кат. 6
TB1	5	розетка ТВ	950	коаксиальный RG-6
LAN1	5	розетка LAN (RJ45)	950	U/UTP кат. 6
ЩС**	8	щит слаботочный	1700	ввод пров.
ДФ1	8	домофон (трубка)	1500	по системе
AP1**	8	точка доступа Wi-Fi		U/UTP кат. 6
LAN3**	10	розетка LAN (RJ45)	300	U/UTP кат. 5e/6

Условные обозначения

- ЩС — щит слаботочный: ввод провайдера, роутер, коммутатор
- ПК — розетка компьютерная RJ45
- ТВ — розетка телевизионная
- ДФ — трубка или монитор домофона
- Wi — точка доступа Wi-Fi (питание PoE)
- кабель от ЩС до точки, отдельным лучом
- мебель и сантехприборы — подложка
- (1) — номер помещения, площадь м²

Допущения и предложения на листе

Основа листа: размеры и контуры этажей подобраны проектировщиком по составу помещений и площадям этажей с картинки 470 px (размеры на ней не читаются); обмер и исходный проект — задание (К-1); высоты: 1-й этаж 2800 мм, мансарда 2700 мм (горизонтальная часть) приняты; скаты кровли мансарды приняты по картинке: колено 1200 мм, уклон 45°, конёк вдоль длинной стороны; проект КР — задание (К-2); наружные стены 400 мм, перегородки 120 мм приняты (К-1); разрешённая мощность 15 кВт принята по типовым ТУ для частного дома (К-4); подрайон климата не задан — принят не северный (жилые от 2,5 м) (К-7).

Знак «**» — предложение проектировщика, заказчиком не утверждено (согласовать с заказчиком): записи в реестре нет: ЩС — щит слаботочный: место и состав; AP1 — точка доступа Wi-Fi: число и места; LAN3 — розетка LAN у рабочего стола.

См. лист открытых вопросов (лист 7, записи К-1, К-2, К-4, К-7).

Примечания

1. За отметку 0,000 принят уровень чистого пола. Высоты H — от чистого пола до оси изделия; привязки — от чистовой грани стены до оси механизма (у рамки на несколько постов — до оси рамки).
2. Высота установки, не указанная на плане: розетки LAN и ТВ — 300 мм от чистого пола.
3. Слаботочные кабели — отдельно от силовых: в своей трубе или лотке, при параллельной прокладке не ближе 100 мм к силовым, пересечения под прямым углом; каждую точку — отдельным кабелем от ЩС** без скруток.
4. Трассы на листе — принципиальные; фактические зафиксировать исполнительной схемой до закрытия отделкой. Силовые линии, УЗО 30 мА, ДСУП, кабель нг(A)-LS — по листам розеток и щита.
5. Проект силовой части и расчёт токов КЗ — по проекту ЭОМ; слаботочная часть согласуется с провайдером и управляющей компанией (домофон, коллективное ТВ).

1000 мм · печать 1:1

Изм.	Кол.уч	Лист	№ док.	Подп.	Дата
Разраб.		Кырлан А.С.			21.10.26
Пров.					
ГИП					
Н. контр.					
Утв.					

ГД-2026-010-АИ

Дом 331 м²

Общая площадь 270,67* м² · * размеры приняты, не замерены (реестр — л. 7, К-1)

Дизайн-проект интерьера

Стадия	Лист	Листов
РП	43	159

План слаботочных сетей · 1-й этаж

М 1:100

Кырлан Александр Сергеевич

выпуск 18.10.2026 № 9365d64cec · стр. 47 из 197

План слаботочных сетей · Мансарда

Интернет, ТВ, домофон · размеры в мм · высоты от чистого пола

ПРЕДВАРИТЕЛЬНО · не для производства работ · открыто пунктов: 6 (реестр — л. 7)

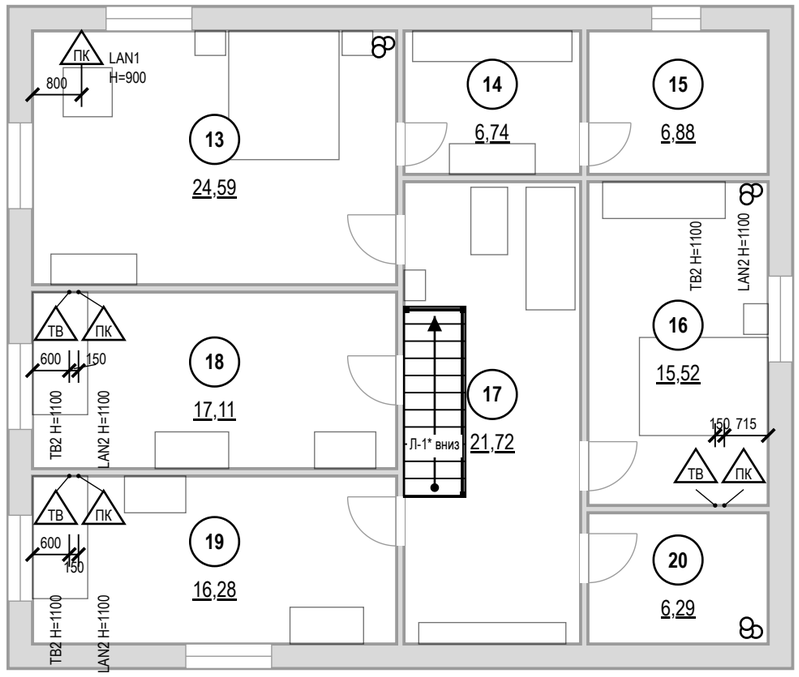

Ведомость слаботочных точек

Марка	Пом.	Назначение	H, мм	Кабель
LAN1	13	розетка LAN (RJ45)	900	U/UTP кат. 6
TB2	16	розетка ТВ	1100	RG-6
LAN2	16	розетка LAN (RJ45)	1100	U/UTP кат. 6
TB2	18	розетка ТВ	1100	RG-6
LAN2	18	розетка LAN (RJ45)	1100	U/UTP кат. 6
TB2	19	розетка ТВ	1100	RG-6
LAN2	19	розетка LAN (RJ45)	1100	U/UTP кат. 6

Условные обозначения

ПК — розетка компьютерная RJ45

ТВ — розетка телевизионная

мебель и сантехприборы — подложка

(1) — номер помещения, площадь м²

Допущения и предложения на листе

Основа листа: размеры и контуры этажей подобраны проектировщиком по составу помещений и площадям этажей с картинки 470 px (размеры на ней не читаются); обмер и исходный проект — задание (К-1); высоты: 1-й этаж 2800 мм, мансарда 2700 мм (горизонтальная часть) приняты; скаты кровли мансарды приняты по картинке: колено 1200 мм, уклон 45°, конёк вдоль длинной стороны; проект КР — задание (К-2); наружные стены 400 мм, перегородки 120 мм приняты (К-1); разрешённая мощность 15 кВт принята по типовым ТУ для частного дома (К-4); подрайон климата не задан — принят не северный (жилые от 2,5 м) (К-7).

Знак «*» — принято, не замерено и не подтверждено (замерить на объекте): К-6: Л-1 — габарит марша снят с картинки заказчика (11 проступей в холле 3,6 м), а до отм. +3,150 нужно 18 подъёмов — одномаршевая не встаёт: решение по К-6.

Знак «**» — предложение проектировщика, заказчиком не утверждено (согласовать с заказчиком): записи в реестре нет: ЩС — щит слаботочный: место и состав.

См. лист открытых вопросов (лист 7, записи К-1, К-2, К-4, К-6, К-7).

Примечания

1. За отметку 0,000 принят уровень чистого пола. Высоты H — от чистого пола до оси изделия; привязки — от чистовой грани стены до оси механизма (у рамки на несколько постов — до оси рамки).
2. Высота установки, не указанная на плане: розетки LAN и ТВ — 300 мм от чистого пола.
3. Слаботочные кабели — отдельно от силовых: в своей трубе или лотке, при параллельной прокладке не ближе 100 мм к силовым, пересечения под прямым углом; каждую точку — отдельным кабелем от ЩС** без скруток.
4. Трассы на листе — принципиальные; фактические зафиксировать исполнительной схемой до закрытия отделкой. Силовые линии, УЗО 30 мА, ДСУП, кабель нг(А)-LS — по листам розеток и щита.
5. Проект силовой части и расчёт токов КЗ — по проекту ЭОМ; слаботочная часть согласуется с провайдером и управляющей компанией (домофон, коллективное ТВ).

1000 мм · печать 1:1

Изм.	Кол.уч	Лист	№ док.	Подп.	Дата
Разраб.		Кырлан А.С.			21.10.26
Пров.					
ГИП					
Н. контр.					
Утв.					

ГД-2026-010-АИ

Дом 331 м²

Общая площадь 270,67* м² · * размеры приняты, не замерены (реестр — л. 7, К-1)

Дизайн-проект интерьера

Стадия	Лист	Листов
РП	44	159

План слаботочных сетей · Мансарда

М 1:100

Кырлан Александр Сергеевич

выпуск 18.10.2026 № 9365d64cec · стр. 48 из 197

План вентиляции · 1-й этаж

Вытяжка, приток, переток · кондиционирование не предусмотрено · размеры в мм · высоты от чистого пола

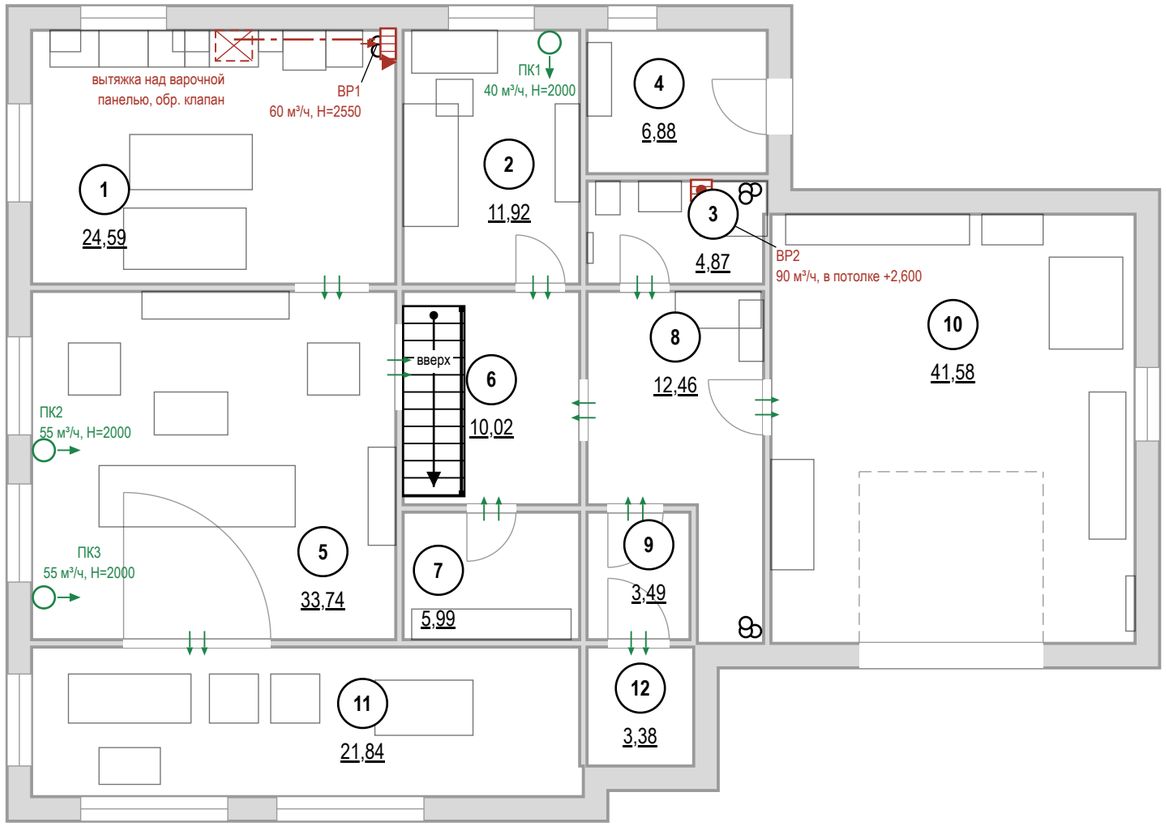

Допущения и предложения на листе

Основа листа: размеры и контуры этажей подобраны проектировщиком по составу помещений и площадям этажей с картинки 470 px (размеры на ней не читаются); обмер и исходный проект — задание (К-1); высоты: 1-й этаж 2800 мм, мансарда 2700 мм (горизонтальная часть) приняты; скаты кровли мансарды приняты по картинке: колено 1200 мм, уклон 45°, конёк вдоль длинной стороны; проект КР — задание (К-2); наружные стены 400 мм, перегородки 120 мм приняты (К-1); разрешённая мощность 15 кВт принята по типовым ТУ для частного дома (К-4); подрайон климата не задан — принят не северный (жилые от 2,5 м) (К-7).

См. лист открытых вопросов (лист 7, записи К-1, К-2, К-4, К-7).

Примечания

1. Расчёт систем ОВ и подбор оборудования — проектная организация с допуском СРО; лист даёт места, трассы и привязки.
2. Нормы вытяжки — СП 54.13330.2022 (Изм. 1, 2), табл. 7.1: кухня с электроплитой 60 м³/ч, с газовой 100; ванная и совмещённый санузел 50; уборная 25; гардеробная 0,2 ч⁻¹. Приток в жилые — 3 м³/ч на 1 м² (менее 20 м² общей площади на человека), иначе 30 м³/ч на человека.
3. Вентканалы и шахты не сужать, не переносить и не закрывать; вентилятор и кухонная вытяжка — через обратный клапан, без перекрытия естественной тяги.
4. Проектные расходы — не ниже нормы, вытяжка сведена с притоком вентиляторами мокрых помещений. Клапаны — в простенке у окна, центр 2000 мм, не над кроватью, не ближе 300 мм к стоякам отопления; типоразмер — на расход.
5. Под подшивным потолком вытяжка — в потолке, воздуховодом за потолком до канала. Кухонная вытяжка в воздухообмен не включена: воздуховод не менее Ø125 в коробе, вход в канал отдельный.
6. Переток — зазор под полотнами межкомнатных дверей или переточная решётка.
7. Кондиционирование заданием не предусмотрено; при установке трассы фреона и дренажа (не менее 40 мм/м, в К1 через сифон) и питание заложить до черновых работ.
8. Привязки оборудования — по паспортам приобретённых моделей, до черновых работ.

1000 мм · печать 1:1

ПРЕДВАРИТЕЛЬНО · не для производства работ · открыто пунктов: 6 (реестр — л. 7)

Условные обозначения

- стояк: К1 — канализация, В1 — ХВС, Т3 — ГВС
- 1 — номер помещения, площадь м²
- вытяжная решётка в венткanал: марка, расход м³/ч, Н центра от чистого пола
- вентилятор с обратным клапаном в подшивном потолке, воздуховод за потолком до канала
- приточный клапан (КИВ) в наружной стене: марка, расход, Н центра
- переток: зазор под полотном или переточная решётка
- кухонная вытяжка над варочной панелью
- воздуховод кухонной вытяжки в коробе под потолком
- отдельный вход воздуховода в венткanал, обратный клапан

Воздухообмен, м³/ч

№	Помещение	Выт. норма	Выт. проект	Прит. норма	Прит. проект	Устройства
1	Кухня-столовая	60	60			ВР1
2	Кабинет-гостевая			36	40	ПК1
3	Санузел 1 этажа	50	90			ВР2
4	Котельная	4				переток
5	Гостиная			102	110	ПК2, ПК3
7	Кладовая	3				переток
10	Гараж	23				переток
	Итого	**140**	**150**	**120**	**150**	

Воздухообмен квартиры — по большей из сумм притока и вытяжки: норма 140 м³/ч, проект 150 м³/ч.
Вытяжка не меньше притока — баланс сведён.

Изм.	Кол.уч	Лист	№ док.	Подп.	Дата
Разраб.		Кырлан А.С.			21.10.26
Пров.					
ГИП					
Н. контр.					
Утв.					

ГД-2026-010-АИ

Дом 331 м²

Общая площадь 270,67* м² · * размеры приняты, не замерены (реестр — л. 7, К-1)

Дизайн-проект интерьера

Стадия	Лист	Листов
РП	45	159

План вентиляции · 1-й этаж

М 1:100

Кырлан Александр Сергеевич

выпуск 18.10.2026 № 9365d64cec · стр. 49 из 197

План вентиляции · Мансарда

Вытяжка, приток, переток · кондиционирование не предусмотрено · размеры в мм · высоты от чистого пола

ПРЕДВАРИТЕЛЬНО · не для производства работ · открыто пунктов: 6 (реестр — л. 7)

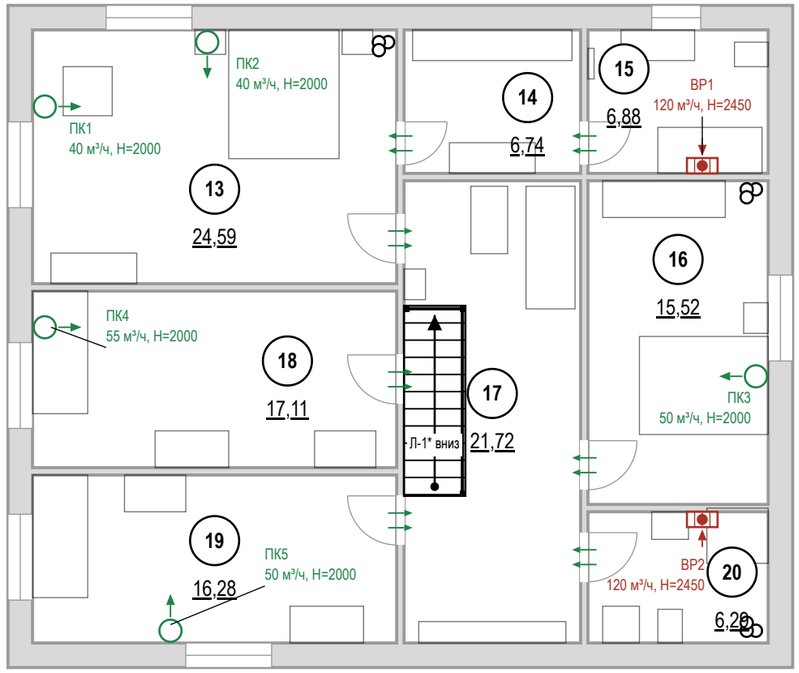

Условные обозначения

- стояк: К1 — канализация, В1 — ХВС, Т3 — ГВС
- 1 — номер помещения, площадь м²
- вытяжная решётка с бытовым вентилятором и обратным клапаном: марка, расход, Н
- приточный клапан (КИВ) в наружной стене: марка, расход, Н центра
- переток: зазор под полотном или переточная решётка

Воздухообмен, м³/ч

№	Помещение	Выт. норма	Выт. проект	Прит. норма	Прит. проект	Устройства
13	Спальня мастер			74	80	ПК1, ПК2
14	Гардеробная мастер	4				переток
15	Санузел мастер	50	120			ВР1
16	Спальня 2			47	50	ПК3
18	Спальня 3			52	55	ПК4
19	Спальня 4			49	50	ПК5
20	Санузел 2	50	120			ВР2
	Итого	**104**	**240**	**120**	**235**	

Воздухообмен квартиры — по большей из сумм притока и вытяжки: норма 120 м³/ч, проект 240 м³/ч.
Вытяжка не меньше притока — баланс сведён.

Допущения и предложения на листе

Основа листа: размеры и контуры этажей подобраны проектировщиком по составу помещений и площадям этажей с картинки 470 px (размеры на ней не читаются); обмер и исходный проект — задание (К-1); высоты: 1-й этаж 2800 мм, мансарда 2700 мм (горизонтальная часть) приняты; скаты кровли мансарды приняты по картинке: колено 1200 мм, уклон 45°, конёк вдоль длинной стороны; проект КР — задание (К-2); наружные стены 400 мм, перегородки 120 мм приняты (К-1); разрешённая мощность 15 кВт принята по типовым ТУ для частного дома (К-4); подрайон климата не задан — принят не северный (жилые от 2,5 м) (К-7).
Знак «*» — принято, не замерено и не подтверждено (замерить на объекте): К-6: Л-1 — габарит марша снят с картинки заказчика (11 проступей в холле 3,6 м), а до отм. +3,150 нужно 18 подъёмов — одномаршевая не встаёт: решение по К-6.
См. лист открытых вопросов (лист 7, записи К-1, К-2, К-4, К-6, К-7).

Примечания

1. Расчёт систем ОВ и подбор оборудования — проектная организация с допуском СРО; лист даёт места, трассы и привязки.
2. Нормы вытяжки — СП 54.13330.2022 (Изм. 1, 2), табл. 7.1: кухня с электроплитой 60 м³/ч, с газовой 100; ванная и совмещённый санузел 50; уборная 25; гардеробная 0,2 ч⁻¹. Приток в жилые — 3 м³/ч на 1 м² (менее 20 м² общей площади на человека), иначе 30 м³/ч на человека.
3. Вентканалы и шахты не сужать, не переносить и не закрывать; вентилятор и кухонная вытяжка — через обратный клапан, без перекрытия естественной тяги.
4. Проектные расходы — не ниже нормы, вытяжка сведена с притоком вентиляторами мокрых помещений. Клапаны — в простенке у окна, центр 2000 мм, не над кроватью, не ближе 300 мм к стоякам отопления; типоразмер — на расход.
5. Переток — зазор под полотнами межкомнатных дверей или переточная решётка.
6. Кондиционирование заданием не предусмотрено; при установке трассы фреона и дренажа (не менее 40 мм/м, в К1 через сифон) и питание заложить до черновых работ.
7. Привязки оборудования — по паспортам приобретённых моделей, до черновых работ.

1000 мм · печать 1:1

Изм.	Кол.уч	Лист	№ док.	Подп.	Дата
Разраб.		Кырлан А.С.			21.10.26
Пров.					
ГИП					
Н. контр.					
Утв.					

ГД-2026-010-АИ

Дом 331 м²

Общая площадь 270,67* м² · * размеры приняты, не замерены (реестр — л. 7, К-1)

Дизайн-проект интерьера

Стадия	Лист	Листов
РП	46	159

План вентиляции · Мансарда

М 1:100

Кырлан Александр Сергеевич

выпуск 18.10.2026 № 9365d64cec · стр. 50 из 197

План отопления · 1-й этаж

Радиаторы, стояки, подводки · размеры в мм · высоты от чистого пола

ПРЕДВАРИТЕЛЬНО · не для производства работ · открыто пунктов: 6 (реестр — л. 7)

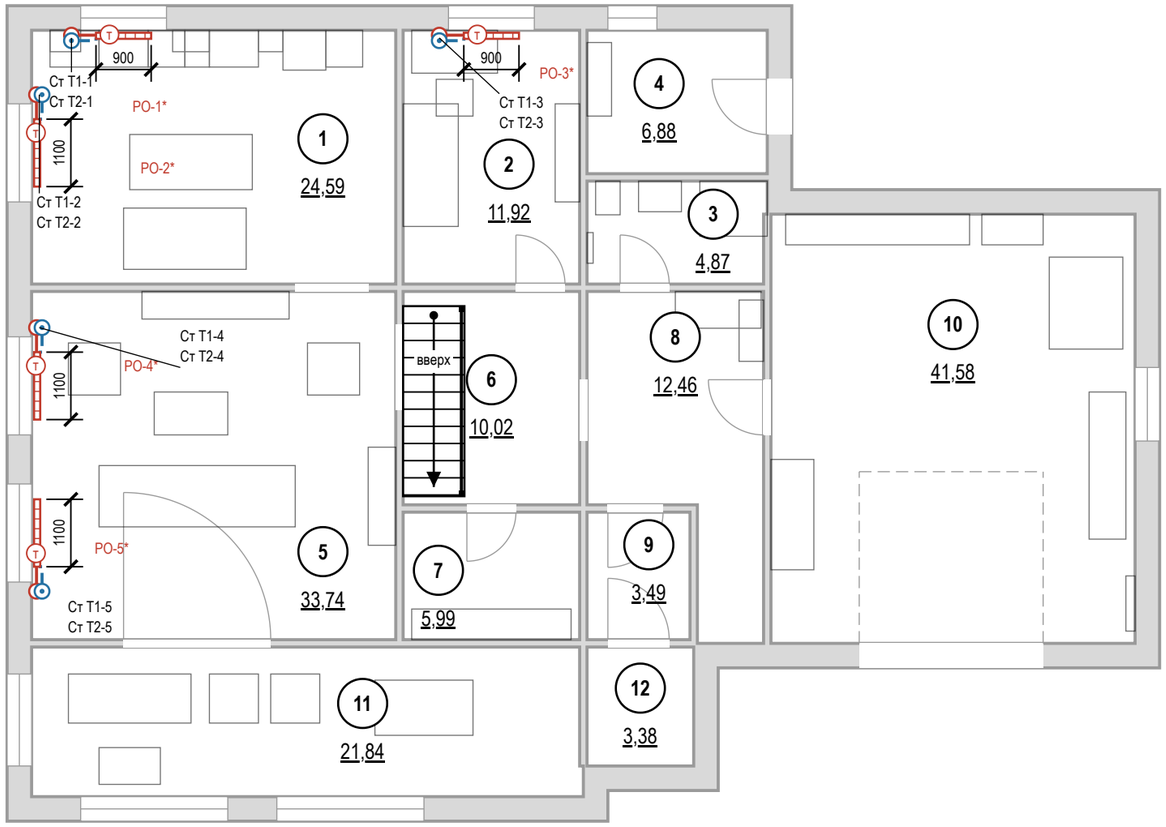

Условные обозначения

- (1) — номер помещения, площадь м²
- радиатор отопления (марка РО-N, длина по плану)
- (Т) — клапан с термоголовкой на подаче
- стояк отопления, подающий (Ст Т1-N)
- стояк отопления, обратный (Ст Т2-N)
- Т1 — отопление, подающий трубопровод
- Т2 — отопление, обратный трубопровод

Ведомость радиаторов

Марка	Помещение	Тип	Д×В×Г, мм	Низ / стена	Q, Вт
РО-1	1. Кухня-столовая	панельный*	900×600×100	120 / 40	расч.
РО-2	1. Кухня-столовая	панельный*	1100×600×100	120 / 40	расч.
РО-3	2. Кабинет-гостевая	панельный*	900×600×100	120 / 40	расч.
РО-4	5. Гостиная	панельный*	1100×600×100	120 / 40	расч.
РО-5	5. Гостиная	панельный*	1100×600×100	120 / 40	расч.

* тип и мощность — по теплотехническому расчёту
Низ — от чистого пола, стена — зазор до задней панели, мм.

Привязки — до обмера
Стояки отопления в исходных данных не заданы: показаны у откосов окон, подводки — принципиально. До черновых работ — обмер стояков и паспорта приборов; лист перевыпустить по факту.

Примечания

1. Расчёт системы отопления, теплопотерь и подбор приборов — проектная организация с допуском СРО; лист даёт места и привязки.
2. Тип, длина и мощность радиаторов — по теплотехническому расчёту; лист задаёт места, зазоры и подключение.
3. Радиаторы — под каждым окном жилых комнат и кухни, центр по оси проёма, длина 0,7 ширины окна (кратно 100); окончательно — по расчёту.
4. Зазоры радиатора: низ не менее 100 мм от чистого пола, верх не менее 100 мм до подоконника, 30–50 мм от стены до задней панели; центр по оси окна с допуском ±20 мм.
5. Радиаторы не закрывать глухими коробами и мебелью; перенос и замена приборов в многоквартирном доме — переустройство, согласование с управляющей организацией (ЖК РФ ст. 25–26); вынос на лоджию запрещён.
6. Трубы отопления через межквартирные стены не прокладывать (СП 51.13330.2011, п. 9.19); через перекрытия и перегородки — в гильзах.
7. Привязки приборов и подводок — по паспортам приобретённых радиаторов и клапанов, до черновых работ.
8. До закрытия отделкой трубопроводы отопления испытать гидростатическим давлением с оформлением акта (СП 73.13330.2016, 7.2–7.3).

Допущения и предложения на листе
Основа листа: размеры и контуры этажей подобраны проектировщиком по составу помещений и площадям этажей с картинки 470 px (размеры на ней не читаются); обмер и исходный проект — задание (К-1); высоты: 1-й этаж 2800 мм, мансарда 2700 мм (горизонтальная часть) приняты; скаты кровли мансарды приняты по картинке: колено 1200 мм, уклон 45°, конёк вдоль длинной стороны; проект КР — задание (К-2); наружные стены 400 мм, перегородки 120 мм приняты (К-1); разрешённая мощность 15 кВт принята по типовым ТУ для частного дома (К-4); подрайон климата не задан — принят не северный (жилые от 2,5 м) (К-7).
См. лист открытых вопросов (лист 7, записи К-1, К-2, К-4, К-7).

1000 мм · печать 1:1

Изм.	Кол.уч	Лист	№ док.	Подп.	Дата
Разраб.		Кырлан А.С.			21.10.26
Пров.					
ГИП					
Н. контр.					
Утв.					

ГД-2026-010-АИ

Дом 331 м²

Общая площадь 270,67* м² · * размеры приняты, не замерены (реестр — л. 7, К-1)

Дизайн-проект интерьера

Стадия	Лист	Листов
РП	47	159

План отопления · 1-й этаж

М 1:100

Кырлан Александр Сергеевич

выпуск 18.10.2026 № 9365d64cec · стр. 51 из 197

План отопления · Мансарда

Радиаторы, стояки, подводки · размеры в мм · высоты от чистого пола

ПРЕДВАРИТЕЛЬНО · не для производства работ · открыто пунктов: 6 (реестр — л. 7)

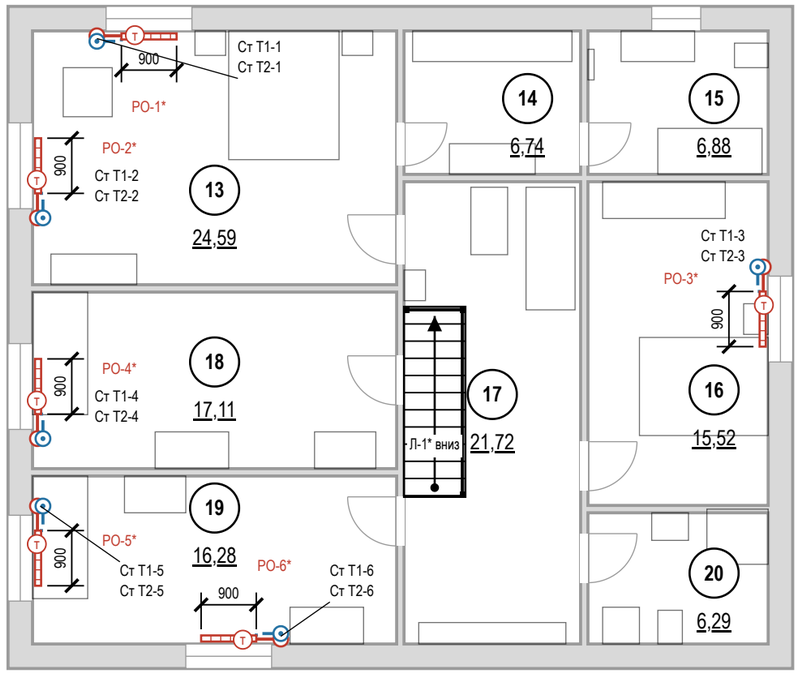

Условные обозначения

- (1) — номер помещения, площадь м²
- радиатор отопления (марка РО-N, длина по плану)
- (T) — клапан с термоголовкой на подаче
- стояк отопления, подающий (Ст Т1-N)
- стояк отопления, обратный (Ст Т2-N)
- Т1 — отопление, подающий трубопровод
- Т2 — отопление, обратный трубопровод

Ведомость радиаторов

Марка	Помещение	Тип	Д×В×Г, мм	Низ / стена	Q, Вт
РО-1	13. Спальня мастер	панельный*	900×600×100	120 / 40	расч.
РО-2	13. Спальня мастер	панельный*	900×600×100	120 / 40	расч.
РО-3	16. Спальня 2	панельный*	900×600×100	120 / 40	расч.
РО-4	18. Спальня 3	панельный*	900×600×100	120 / 40	расч.
РО-5	19. Спальня 4	панельный*	900×600×100	120 / 40	расч.
РО-6	19. Спальня 4	панельный*	900×600×100	120 / 40	расч.

* тип и мощность — по теплотехническому расчёту
Низ — от чистого пола, стена — зазор до задней панели, мм.

Привязки — до обмера
Стояки отопления в исходных данных не заданы: показаны у откосов окон, подводки — принципиально. До черновых работ — обмер стояков и паспорта приборов; лист перевыпустить по факту.

Примечания

1. Расчёт системы отопления, теплопотерь и подбор приборов — проектная организация с допуском СРО; лист даёт места и привязки.
2. Тип, длина и мощность радиаторов — по теплотехническому расчёту; лист задаёт места, зазоры и подключение.
3. Радиаторы — под каждым окном жилых комнат и кухни, центр по оси проёма, длина 0,7 ширины окна (кратно 100); окончательно — по расчёту.
4. Зазоры радиатора: низ не менее 100 мм от чистого пола, верх не менее 100 мм до подоконника, 30–50 мм от стены до задней панели; центр по оси окна с допуском ±20 мм.
5. Радиаторы не закрывать глухими коробами и мебелью; перенос и замена приборов в многоквартирном доме — переустройство, согласование с управляющей организацией (ЖК РФ ст. 25–26); вынос на лоджию запрещён.
6. Трубы отопления через межквартирные стены не прокладывать (СП 51.13330.2011, п. 9.19); через перекрытия и перегородки — в гильзах.
7. Привязки приборов и подводок — по паспортам приобретённых радиаторов и клапанов, до черновых работ.
8. До закрытия отделкой трубопроводы отопления испытать гидростатическим давлением с оформлением акта (СП 73.13330.2016, 7.2–7.3).

Допущения и предложения на листе
Основа листа: размеры и контуры этажей подобраны проектировщиком по составу помещений и площадям этажей с картинки 470 px (размеры на ней не читаются); обмер и исходный проект — задание (К-1); высоты: 1-й этаж 2800 мм, мансарда 2700 мм (горизонтальная часть) приняты; скаты кровли мансарды приняты по картинке: колено 1200 мм, уклон 45°, конёк вдоль длинной стороны; проект КР — задание (К-2); наружные стены 400 мм, перегородки 120 мм приняты (К-1); разрешённая мощность 15 кВт принята по типовым ТУ для частного дома (К-4); подрайон климата не задан — принят не северный (жилые от 2,5 м) (К-7).
Знак «*» — принято, не замерено и не подтверждено (замерить на объекте): К-6: Л-1 — габарит марша снят с картинки заказчика (11 проступей в холле 3,6 м), а до отм. +3,150 нужно 18 подъёмов — одномаршевая не встаёт: решение по К-6.
См. лист открытых вопросов (лист 7, записи К-1, К-2, К-4, К-6, К-7).

1000 мм · печать 1:1

Изм.	Кол.уч	Лист	№ док.	Подп.	Дата
Разраб.		Кырлан А.С.			21.10.26
Пров.					
ГИП					
Н. контр.					
Утв.					

ГД-2026-010-АИ

Дом 331 м²

Общая площадь 270,67* м² · * размеры приняты, не замерены (реестр — л. 7, К-1)

Дизайн-проект интерьера

Стадия	Лист	Листов
РП	48	159

План отопления · Мансарда

М 1:100

Кырлан Александр Сергеевич

выпуск 18.10.2026 № 9365d64cec · стр. 52 из 197

План выводов сантехники · 1-й этаж

Выводы В1, Т3, К1 · привязки от чистовых стен · высоты от чистого пола, мм

ПРЕДВАРИТЕЛЬНО · не для производства работ · открыто пунктов: 6 (реестр — л. 7)

Фрагмент 1. Санузел 1 этажа (пом. 3)

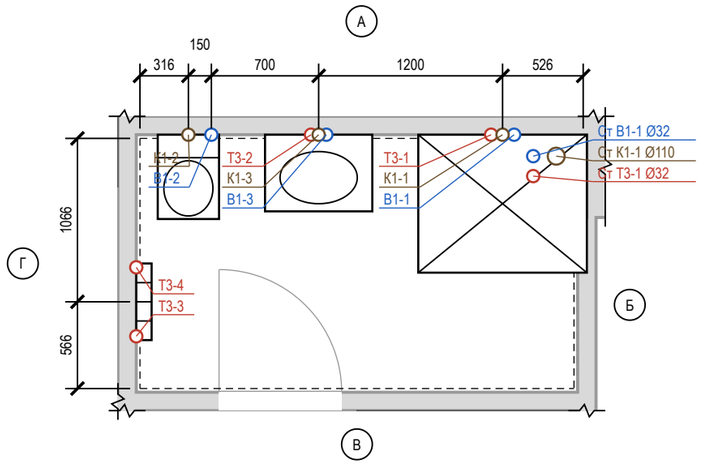

Фрагмент 2. Кухня-столовая (пом. 1)

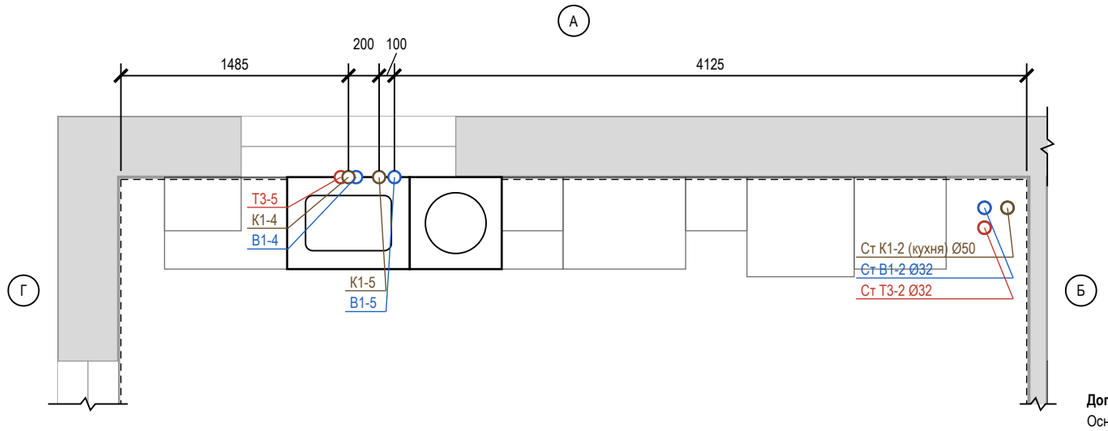

Ведомость привязок выводов

Код	Прибор	Ø	H, мм	Привязка от чист. стен, мм	Прим.
В1-1	Сн1 душ	½"	1200*	ст. А: 451 от Б	межос. 150
Т3-1	Сн1 душ	½"	1200*	ст. А: 601 от Б	межос. 150
К1-1	Сн1 душ	Ø50	70*	ст. А: 526 от Б	сифон поддона
В1-2	Сн2 унитаз подвесной	½"	250*	ст. А: 466 от Г	в раме инсталляции
К1-2	Сн2 унитаз подвесной	Ø110	220*	ст. А: 316 от Г	
В1-3	Сн3 умывальник	½"	600*	ст. А: 1216 от Г	межос. 100
Т3-2	Сн3 умывальник	½"	600*	ст. А: 1116 от Г	межос. 100
К1-3	Сн3 умывальник	Ø50	500*	ст. А: 1166 от Г	
Т3-3	Сн4 полотенцесушитель	½"	1150*	ст. Г: 341 от В	подача, межос. 450; байпас и краны
Т3-4	Сн4 полотенцесушитель	½"	1150*	ст. Г: 791 от В	обратка
В1-4	П5 мойка кухонная	½"	600*	ст. А: 1535 от Г	межос. 100
Т3-5	П5 мойка кухонная	½"	600*	ст. А: 1435 от Г	межос. 100
К1-4	П5 мойка кухонная	Ø50	400*	ст. А: 1485 от Г	
В1-5	П6 посудомоечная машина	½"	550*	ст. А: 1785 от Г	кран ПММ в шкафу мойки
К1-5	П6 посудомоечная машина	Ø40	550*	ст. А: 1685 от Г	слив ПММ в шкафу мойки

* — высота по практике монтажа; сверить по паспорту прибора

Условные обозначения

- вывод В1 (код — в ведомости привязок)
- вывод Т3 (код — в ведомости привязок)
- вывод К1 (код — в ведомости привязок)
- сантехприбор по расстановке (габарит модели)
- чистовая поверхность стены (от неё привязки)
- стояк «Ст К1-N / Ст В1-N» (ГОСТ 21.601), Ø мм
- линия обрыва (граница фрагмента)
- А — обозначение стены А–Г (как на развёртках)

Примечания

1. Привязки выводов даны от чистовых поверхностей стен (облицовка на сторону: санузел 1 этажа — 24 мм (штукатурка 10 + клей 5 + плитка 9); кухня-столовая — 22 мм (фартук: штукатурка 10 + клей 3 + плитка 9)); эти же грани — на развёртках и в раскладке плитки. Высоты — от чистого пола помещения.
2. Высоты и межосевые, отмеченные «*», приняты по практике монтажа; до черновой разводки сверить по паспорту выбранного прибора (смеситель, инсталляция, сифон).
3. Горячая вода (Т3) — слева от холодной (В1), если смотреть на прибор. Допуск установки выводов: ±5 мм в группе, ±20 мм у отдельно стоящих.
4. Расчёт систем водоснабжения и канализации и подбор оборудования выполняет проектная организация; лист задаёт места и высоты выводов.
5. Посудомоечная машина П6: кран и слив — отдельными выводами в шкафу мойки (не за машиной), до машины ≤ 1500 мм.
6. Прибор П5 мойка кухонная, П6 посудомоечная машина взят из расстановки мебели (по шкафу с мойкой).
7. Стояки в коробах/шахтах не замоноличивать; стояк К1 в коробе — звукоизоляция стояка в коробе без жёсткого контакта с трубой; к арматуре и ревизиям — люк не меньше 300×400.

1000 мм · печать 1:1

Допущения и предложения на листе

Основа листа: размеры и контуры этажей подобраны проектировщиком по составу помещений и площадям этажей с картинки 470 px (размеры на ней не читаются); обмер и исходный проект — задание (К-1); высоты: 1-й этаж 2800 мм, мансарда 2700 мм (горизонтальная часть) приняты; скаты кровли мансарды приняты по картинке: колено 1200 мм, уклон 45°, конёк вдоль длинной стороны; проект КР — задание (К-2); наружные стены 400 мм, перегородки 120 мм приняты (К-1); разрешённая мощность 15 кВт принята по типовым ТУ для частного дома (К-4); подрайон климата не задан — принят не северный (жилые от 2,5 м) (К-7).
См. лист открытых вопросов (лист 7, записи К-1, К-2, К-4, К-7).

Изм.	Кол.уч	Лист	№ док.	Подп.	Дата			
Разраб.		Кырлан А.С.			21.10.26	ГД-2026-010-АИ		
Пров.						Дом 331 м²		
ГИП						Общая площадь 270,67* м² · * размеры приняты, не замерены (реестр — л. 7, К-1)		
						Дизайн-проект интерьера	Стадия: РП	Лист: 49 / Листов: 159
Н. контр.						План выводов сантехники · 1-й этаж	Кырлан Александр Сергеевич	
Утв.						М 1:40		

выпуск 18.10.2026 № 9365d64cec · стр. 53 из 197

План выводов сантехники · Мансарда

Выводы В1, Т3, К1 · привязки от чистовых стен · высоты от чистого пола, мм

ПРЕДВАРИТЕЛЬНО · не для производства работ · открыто пунктов: 6 (реестр — л. 7)

Фрагмент 1. Санузел мастер (пом. 15)

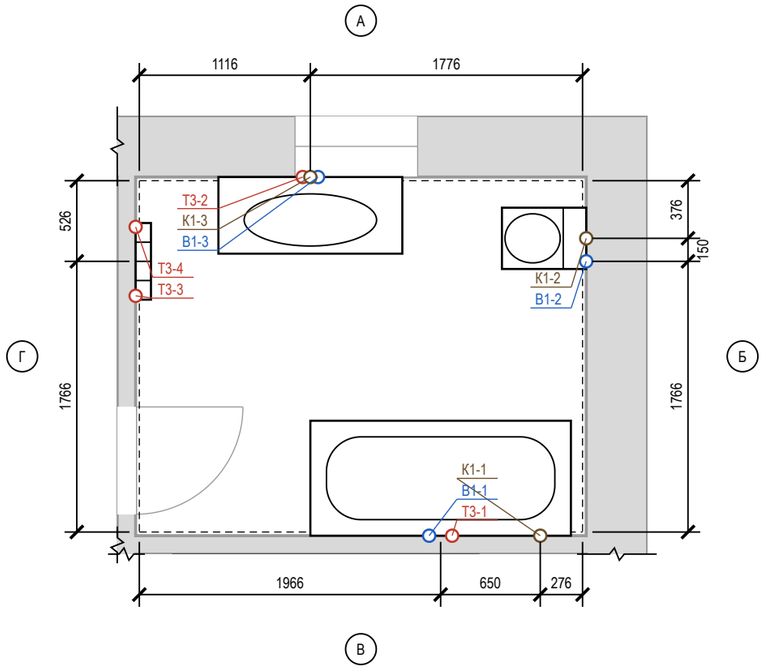

Фрагмент 2. Санузел 2 (пом. 20)

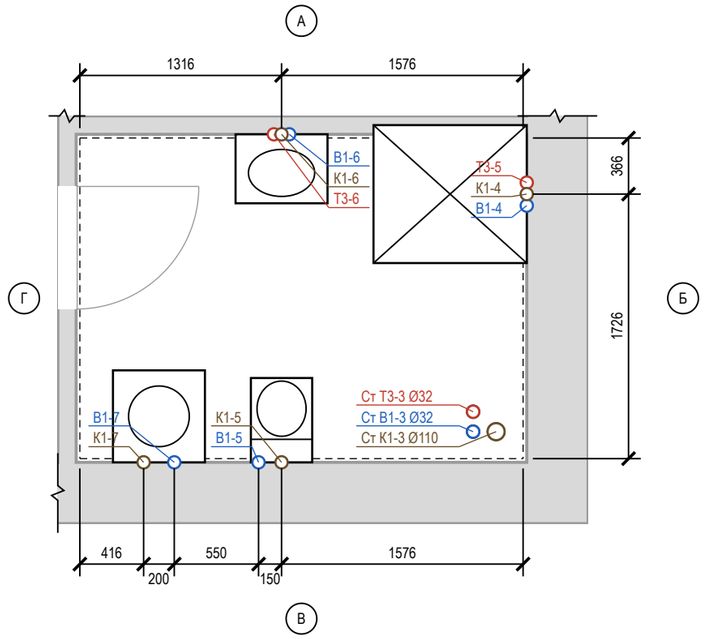

Ведомость привязок выводов

Код	Прибор	Ø	H, мм	Привязка от чист. стен, мм	Прим.
В1-1	См1 ванна	½"	800*	ст. В: 1001 от Б	межос. 150
Т3-1	См1 ванна	½"	800*	ст. В: 851 от Б	межос. 150
К1-1	См1 ванна	Ø50	50*	ст. В: 276 от Б	
В1-2	См2 унитаз подвесной	½"	250*	ст. Б: 526 от А	в раме инсталляции
К1-2	См2 унитаз подвесной	Ø110	220*	ст. Б: 376 от А	
В1-3	См3 умывальник	½"	600*	ст. А: 1166 от Г	межос. 100
Т3-2	См3 умывальник	½"	600*	ст. А: 1066 от Г	межос. 100
К1-3	См3 умывальник	Ø50	500*	ст. А: 1116 от Г	
Т3-3	См4 полотенцесушитель	½"	1150*	ст. Г: 751 от А	подача, межос. 450; байпас и краны
Т3-4	См4 полотенцесушитель	½"	1150*	ст. Г: 301 от А	обратка
В1-4	Сд1 душ	½"	1200*	ст. Б: 441 от А	межос. 150
Т3-5	Сд1 душ	½"	1200*	ст. Б: 291 от А	межос. 150
К1-4	Сд1 душ	Ø50	70*	ст. Б: 366 от А	сифон поддона
В1-5	Сд2 унитаз подвесной	½"	250*	ст. В: 1166 от Г	в раме инсталляции
К1-5	Сд2 унитаз подвесной	Ø110	220*	ст. В: 1316 от Г	
В1-6	Сд3 умывальник	½"	600*	ст. А: 1366 от Г	межос. 100
Т3-6	Сд3 умывальник	½"	600*	ст. А: 1266 от Г	межос. 100
К1-6	Сд3 умывальник	Ø50	500*	ст. А: 1316 от Г	
В1-7	Сд4 стиральная машина	½"	600*	ст. В: 616 от Г	кран машины
К1-7	Сд4 стиральная машина	Ø50	600*	ст. В: 416 от Г	

* — высота по практике монтажа; сверить по паспорту прибора

Условные обозначения

- вывод В1 (код — в ведомости привязок)
- вывод Т3 (код — в ведомости привязок)
- вывод К1 (код — в ведомости привязок)
- сантехприбор по расстановке (габарит модели)
- чистовая поверхность стены (от неё привязки)
- стояк «Ст К1-N / Ст В1-N» (ГОСТ 21.601), Ø мм
- линия обрыва (граница фрагмента)
- обозначение стены А–Г (как на развёртках)

Допущения и предложения на листе

Основа листа: размеры и контуры этажей подобраны проектировщиком по составу помещений и площадям этажей с картинки 470 px (размеры на ней не читаются); обмер и исходный проект — задание (К-1); высоты: 1-й этаж 2800 мм, мансарда 2700 мм (горизонтальная часть) приняты; скаты кровли мансарды приняты по картинке: колено 1200 мм, уклон 45°, конёк вдоль длинной стороны; проект КР — задание (К-2); наружные стены 400 мм, перегородки 120 мм приняты (К-1); разрешённая мощность 15 кВт принята по типовым ТУ для частного дома (К-4); подрайон климата не задан — принят не северный (жилые от 2,5 м) (К-7).

См. лист открытых вопросов (лист 7, записи К-1, К-2, К-4, К-7).

Примечания

1. Привязки выводов даны от чистовых поверхностей стен (облицовка на сторону: санузел мастер — 24 мм (штукатурка 10 + клей 5 + плитка 9); санузел 2 24 мм (штукатурка 10 + клей 5 + плитка 9)); эти же грани — на развёртках и в раскладке плитки. Высоты — от чистого пола помещения.
2. Высоты и межосевые, отмеченные «*», приняты по практике монтажа; до черновой разводки сверить по паспорту выбранного прибора (смеситель, инсталляция, сифон).
3. Горячая вода (Т3) — слева от холодной (В1), если смотреть на прибор. Допуск установки выводов: ±5 мм в группе, ±20 мм у отдельно стоящих.
4. Расчёт систем водоснабжения и канализации и подбор оборудования выполняет проектная организация; лист задаёт места и высоты выводов.
5. Стояки в коробах/шахтах не замоноличивать; стояк К1 в коробе — звукоизоляция стояка в коробе без жёсткого контакта с трубой; к арматуре и ревизиям — люк не меньше 300×400.

1000 мм · печать 1:1

Изм.	Кол.уч	Лист	№ док.	Подп.	Дата
Разраб.		Кырлан А.С.			21.10.26
Пров.					
ГИП					
Н. контр.					
Утв.					

ГД-2026-010-АИ

Дом 331 м²

Общая площадь 270,67* м² · * размеры приняты, не замерены (реестр — л. 7, К-1)

Дизайн-проект интерьера	Стадия	Лист	Листов
	РП	50	159

План выводов сантехники · Мансарда

М 1:40

Кырлан Александр Сергеевич

выпуск 18.10.2026 № 9365d64cec · стр. 54 из 197

Схема разводки водопровода и канализации · 1-й этаж

Схемы систем В1, Т3, К1 · трассы принципиальные · уклоны в мм на 1 м · план М 1:400, фрагменты М 1:25

ПРЕДВАРИТЕЛЬНО · не для производства работ · открыто пунктов: 6 (реестр — л. 7)

План квартиры (М 1:400)

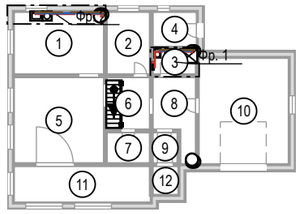

Допущения и предложения на листе

Основа листа: размеры и контуры этажей подобраны проектировщиком по составу помещений и площадям этажей с картинки 470 px (размеры на ней не читаются); обмер и исходный проект — задание (К-1); высоты: 1-й этаж 2800 мм, мансарда 2700 мм (горизонтальная часть) приняты; скаты кровли мансарды приняты по картинке: колено 1200 мм, уклон 45°, конёк вдоль длинной стороны; проект КР — задание (К-2); наружные стены 400 мм, перегородки 120 мм приняты (К-1); разрешённая мощность 15 кВт принята по типовым ТУ для частного дома (К-4); подрайон климата не задан — принят не северный (жилые от 2,5 м) (К-7).

См. лист открытых вопросов (лист 7, записи К-1, К-2, К-4, К-7).

Фр. 1. Санузел 1 этажа (М 1:25)

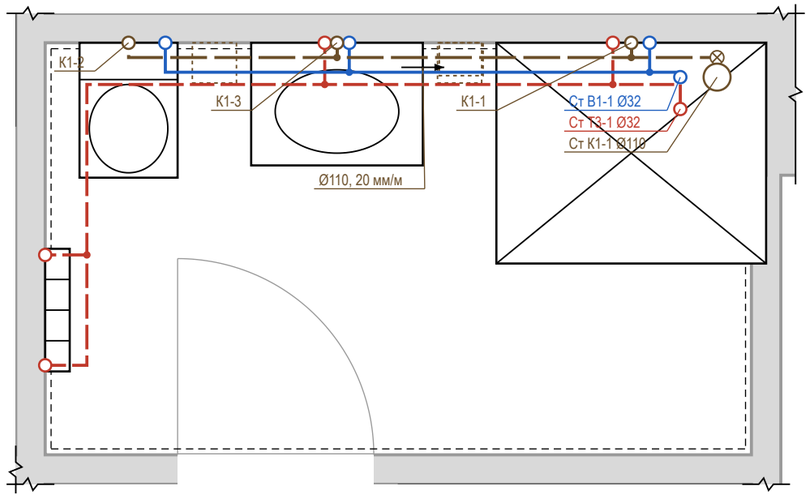

Фр. 2. Кухня-столовая (М 1:25)

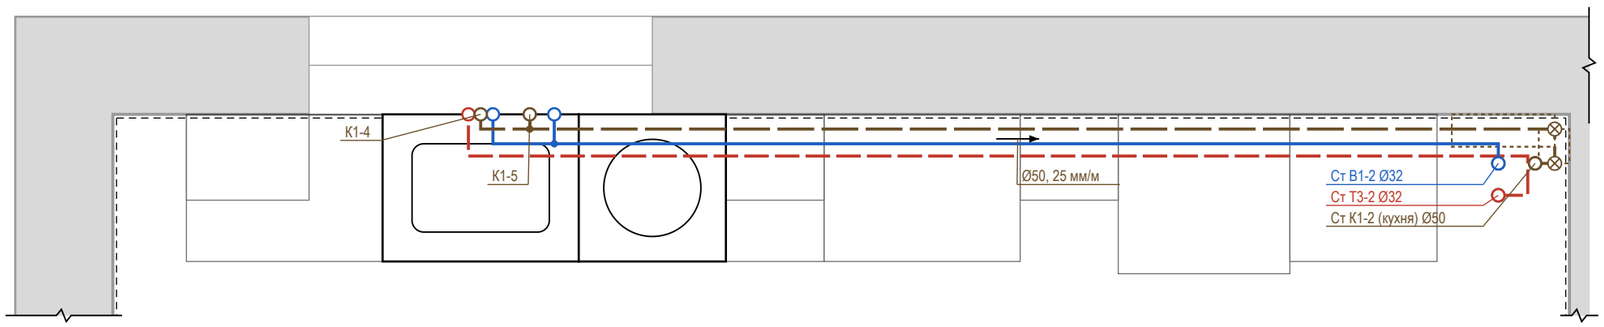

Условные обозначения

- В1 — водопровод хозяйственно-питьевой (ХВС), PP-R Ø20
- Т3 — горячее водоснабжение, подача (ГВС), PP-R Ø20
- К1 — канализация бытовая
- направление уклона К1 / пола: Ø, мм на 1 м
- ⊗ ревизия (прочистка) К1 — доступ сохранить
- • тройник (ответвление к прибору)
- короб К1 над чистым полом (ГКЛВ под плитку)
- ○ вывод В1 (код — в ведомости привязок)
- ○ вывод Т3 (код — в ведомости привязок)
- ○ вывод К1 (код — в ведомости привязок)
- ▭ сантехприбор по расстановке (габарит модели)
- ◯ стояк «Ст К1-N / Ст В1-N» (ГОСТ 21.601), Ø мм
- ∿ линия обрыва (граница фрагмента)
- ▭ граница фрагмента на плане (Фр. N)

Профиль выпусков К1 (до врезки в стояк)

Выпуск	Прибор	Ø	L, м	i, мм/м	Δh, мм	Прокладка, мм
К1-2	Сн2 унитаз подвесной	Ø110	2,54	20	51	короб 200×140
К1-4	П5 мойка кухонная	Ø50	4,66	25	117	короб 200×110
К1-3	Сн3 умывальник	Ø50	1,69	25	42	короб 130×110
К1-1	Сн1 душ	Ø50	0,49	25	12	над полом за приборами
К1-5	П6 посудомоечная машина	Ø40	4,46	30	134	короб 210×110

Короб h×b: h — от чистого пола, b — от чистовой стены. Стяжка 35 мм — лист полов.

Узел ввода В1, Т3 (схема, без масштаба)

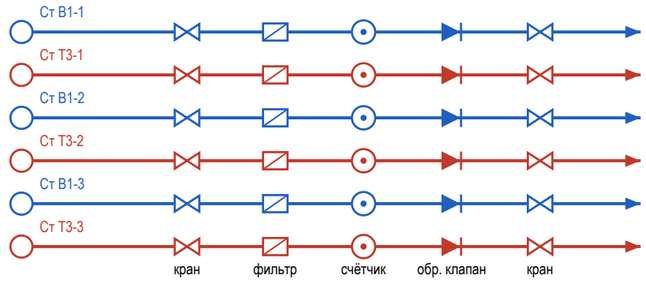

⊗ Ст К1-1, Ст К1-2 (кухня), Ст К1-3: ревизия на стояке — люк в коробе

Примечания

1. Трассы принципиальные, построены от стояков вдоль стен помещений; фактическое положение фиксируется исполнительной схемой с привязками (фото с рулеткой) до закрытия.
2. Уклон К1 не менее 1/d и не более 150 мм/м (СП 30.13330.2020, п. 19.1), приняты практические уклоны; поворот — двумя отводами 45°, ревизия после поворота, доступ сохранить. Стояк К1 в коробе — звукоизоляция стояка в коробе, без жёсткого контакта короба с трубой.
3. Решение по К1: стяжка 35 мм не укрывает трубы (нужно Ø + Δh + 45 мм) — выпуски идут над чистым полом вдоль стен: К1-1 — за приборами и в раме инсталляции; К1-2, К1-4, К1-3, К1-5 — в коробе ГКЛВ под плитку (размеры в профиле). Короба — на развёртках; отметку низа врезки в стояк замерить до черновых работ.
4. На каждом вводе В1 и Т3 — кран шаровой, фильтр, счётчик, обратный клапан; доступ через люк не меньше 300×400. Водопровод — в штробе стен или в коробах; трубы испытать давлением до закрытия (акт скрытых работ).
5. Расчёт систем, диаметры магистралей и подбор оборудования выполняет проектная организация; врезка и перенос стояков — по согласованию с управляющей организацией. Арматуру и привязки сверить по паспортам приборов.

Изм.	Кол.уч	Лист	№ док.	Подп.	Дата
Разраб.		Кырлан А.С.			21.10.26
Пров.					
ГИП					
Н. контр.					
Утв.					

ГД-2026-010-АИ

Дом 331 м²

Общая площадь 270,67* м² · * размеры приняты, не замерены (реестр — л. 7, К-1)

Дизайн-проект интерьера

Стадия	Лист	Листов
РП	51	159

Схема разводки водопровода и канализации · 1-й этаж

М б/м

Кырлан Александр Сергеевич

выпуск 18.10.2026 № 9365d64cec · стр. 55 из 197

Схема разводки водопровода и канализации · Мансарда

ПРЕДВАРИТЕЛЬНО · не для производства работ · открыто пунктов: 6 (реестр — л. 7)

Схемы систем В1, Т3, К1 · трассы принципиальные · уклоны в мм на 1 м · план М 1:200, фрагменты М 1:40

План квартиры (М 1:200)

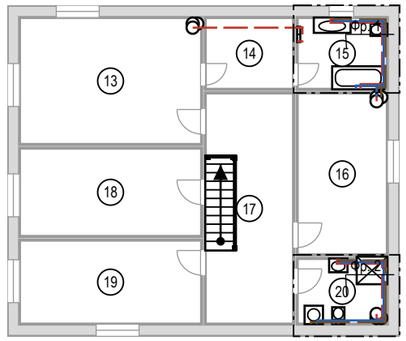

Фр. 1. Санузел мастер (М 1:40)

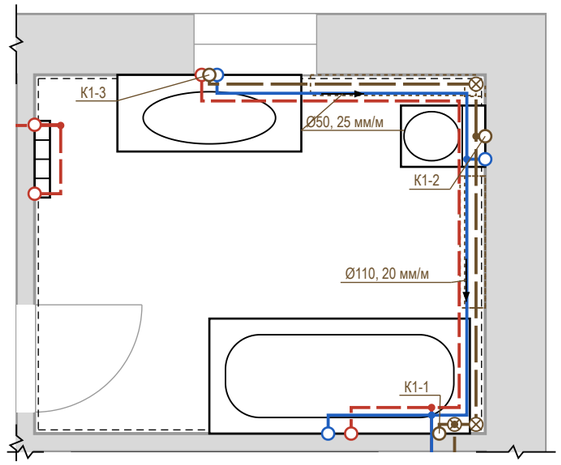

Фр. 2. Санузел 2 (М 1:40)

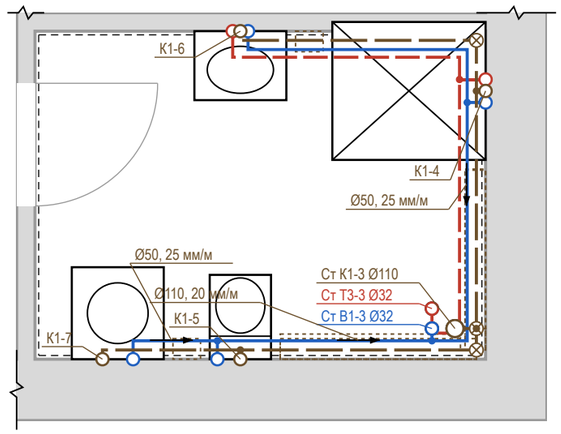

Условные обозначения

- В1 — водопровод хозяйственно-питьевой (ХВС), PP-R Ø20
- Т3 — горячее водоснабжение, подача (ГВС), PP-R Ø20
- К1 — канализация бытовая
- направление уклона К1 / пола: Ø, мм на 1 м
- ревизия (прочистка) К1 — доступ сохранить
- тройник (ответвление к прибору)
- короб К1 над чистым полом (ГКЛВ под плитку)
- вывод В1 (код — в ведомости привязок)
- вывод Т3 (код — в ведомости привязок)
- вывод К1 (код — в ведомости привязок)
- сантехприбор по расстановке (габарит модели)
- стояк «Ст К1-N / Ст В1-N» (ГОСТ 21.601), Ø мм
- линия обрыва (граница фрагмента)
- граница фрагмента на плане (Фр. N)

Профиль выпусков К1 (до врезки в стояк)

Выпуск	Прибор	Ø	L, м	i, мм/м	Δh, мм	Прокладка, мм
К1-2	См2 унитаз подвесной	Ø110	2,40	20	48	короб 190×140
К1-5	Сд2 унитаз подвесной	Ø110	1,88	20	38	короб 180×140
К1-3	См3 умывальник	Ø50	4,48	25	112	короб 200×110
К1-6	Сд3 умывальник	Ø50	3,62	25	91	короб 180×110
К1-7	Сд4 стиральная машина	Ø50	2,78	25	70	короб 150×110
К1-4	Сд1 душ	Ø50	1,75	25	44	короб 130×110
К1-1	См1 ванна	Ø50	0,48	25	12	над полом за приборами

Короб h×b: h — от чистого пола, b — от чистовой стены. Стяжка 35 мм — лист полов.

Узел ввода В1, Т3 (схема, без масштаба)

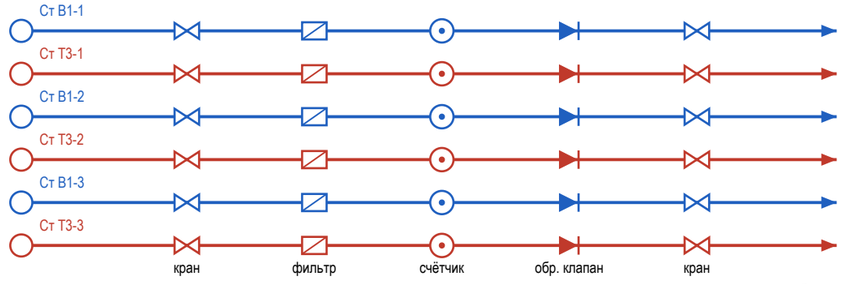

⊗ Ст К1-1, Ст К1-2 (кухня), Ст К1-3: ревизия на стояке — люк в коробе

Допущения и предложения на листе

Основа листа: размеры и контуры этажей подобраны проектировщиком по составу помещений и площадям этажей с картинки 470 px (размеры на ней не читаются); обмер и исходный проект — задание (К-1); высоты: 1-й этаж 2800 мм, мансарда 2700 мм (горизонтальная часть) приняты; скаты кровли мансарды приняты по картинке: колено 1200 мм, уклон 45°, конёк вдоль длинной стороны; проект КР — задание (К-2); наружные стены 400 мм, перегородки 120 мм приняты (К-1); разрешённая мощность 15 кВт принята по типовым ТУ для частного дома (К-4); подрайон климата не задан — принят не северный (жилые от 2,5 м) (К-7).

См. лист открытых вопросов (лист 7, записи К-1, К-2, К-4, К-7).

Примечания

1. Трассы принципиальные, построены от стояков вдоль стен помещений; фактическое положение фиксируется исполнительной схемой с привязками (фото с рулеткой) до закрытия.
2. Уклон К1 не менее 1/d и не более 150 мм/м (СП 30.13330.2020, п. 19.1), приняты практические уклоны; поворот — двумя отводами 45°, ревизия после поворота, доступ сохранить. Стояк К1 в коробе — звукоизоляция стояка в коробе, без жёсткого контакта короба с трубой.
3. Решение по К1: стяжка 35 мм не укрывает трубы (нужно Ø + Δh + 45 мм) — выпуски идут над чистым полом вдоль стен: К1-1 — за приборами и в раме инсталляции; К1-2, К1-5, К1-3, К1-6, К1-7, К1-4 — в коробе ГКЛВ под плитку (размеры в профиле). Короба — на развёртках; отметку низа врезки в стояк замерить до черновых работ.
4. На каждом вводе В1 и Т3 — кран шаровой, фильтр, счётчик, обратный клапан; доступ через люк не меньше 300×400. Водопровод — в штробе стен или в коробах; трубы испытать давлением до закрытия (акт скрытых работ).
5. Расчёт систем, диаметры магистралей и подбор оборудования выполняет проектная организация; врезка и перенос стояков — по согласованию с управляющей организацией. Арматуру и привязки сверить по паспортам приборов.

Изм.	Кол.уч	Лист	№ док.	Подп.	Дата
Разраб.		Кырлан А.С.			21.10.26
Пров.					
ГИП					
Н. контр.					
Утв.					

ГД-2026-010-АИ

Дом 331 м²

Общая площадь 270,67* м² · * размеры приняты, не замерены (реестр — л. 7, К-1)

Дизайн-проект интерьера

Стадия	Лист	Листов
РП	52	159

Схема разводки водопровода и канализации · Мансарда

М б/м

Кырлан Александр Сергеевич

Спецификация сантехнического оборудования

Форма 1 ГОСТ 21.110-2013 · ГД-2026-010-АИ-ВК.СО · приборы, арматура, трубопроводы

ПРЕДВАРИТЕЛЬНО · не для производства работ · открыто пунктов: 6 (реестр — л. 7)

Поз.	Наименование и техническая характеристика	Тип, марка, обозначение документа	Код продукции	Поставщик	Ед. изм.	Кол.	Масса 1 ед., кг	Примечание
	Санитарные приборы							
1	Ванна акриловая 1700×750 мм, с каркасом, экраном и отверстием слив-перелив	аналог		выбор заказчика	шт	1		См1
2	Унитаз подвесной безободковый, с сиденьем микролифт, крепёж и звукоизолирующая прокладка	Jacob Delafon Struktura EDF102-00		выбор заказчика	шт	3		Сн2, См2, Сд2
3	Инсталляция для подвесного унитаза: рама высотой 1120 мм, бачок, клавиша смыва (ось клавиши 1050 мм от чистого пола)	аналог		выбор заказчика	шт	3		Сн2, См2, Сд2; короб ГКЛВ
4	Умывальник подвесной 700×500 мм, с отверстием под смеситель и переливом	аналог		выбор заказчика	шт	1		Сн3
5	Умывальник подвесной 1200×500 мм, с отверстием под смеситель и переливом	аналог		выбор заказчика	шт	1		См3
6	Умывальник подвесной 600×450 мм, с отверстием под смеситель и переливом	аналог		выбор заказчика	шт	1		Сд3
7	Поддон душевой низкий 1100×900 мм, с сифоном и выпуском Ø50, на ножках/подиуме	аналог		выбор заказчика	шт	1		Сн1
8	Поддон душевой низкий 900×1000 мм, с сифоном и выпуском Ø50, на ножках/подиуме	аналог		выбор заказчика	шт	1		Сд1
9	Мойка кухонная 800×600 мм, с переливом	аналог		с кухонной мебелью	шт	1		П13
10	Полотенцесушитель водяной (ГВС), с байпасом и кранами	аналог		выбор заказчика	шт	2		Сн4, См4
	Смесители, сифоны и арматура приборов							
11	Смеситель для ванны настенный однорычажный, межосевое 150 мм, с душевым набором (лейка, шланг, держатель)	аналог		выбор заказчика	шт	1		См1
12	Смеситель для умывальника однорычажный, с донным клапаном	аналог		выбор заказчика	шт	3		Сн3, См3, Сд3
13	Душевая система скрытого монтажа с термостатом: встраиваемая часть, верхний душ, ручная лейка	аналог		выбор заказчика	шт	2		Сн1, Сд1; встраиваемая часть — до плитки
14	Смеситель кухонный однорычажный, высокий излив	аналог		выбор заказчика	шт	1		П13
15	Обвязка ванны слив-перелив Ø40/50 с сифоном	аналог		выбор заказчика	шт	1		См1
16	Сифон для умывальника бутылочный Ø32/40–50, с гофрой к выпуску	аналог		выбор заказчика	шт	3		Сн3, См3, Сд3
17	Сифон для мойки с отводом для ПММ Ø40/50	аналог		выбор заказчика	шт	1		П13
18	Сифон для стиральной машины встраиваемый в стену Ø50, с обратным клапаном	аналог		выбор заказчика	шт	1		Сд4
19	Кран угловой ½"×½" с гибкой подводкой 40 см (умывальники, мойка)	аналог		выбор заказчика	шт	8		по 2 на прибор
20	Кран шаровой угловой ½"×¾" для подключения стиральной и посудомоечной машины	аналог		выбор заказчика	шт	2		Сд4, П14
21	Узел подключения полотенцесушителя: байпас Ду20, краны шаровые ½" ×2	аналог		выбор заказчика	шт	2		
	Трубопроводы							
22	Труба полипропиленовая PP-R PN20 Ø20×3,4 (В1)	ГОСТ 32415-2013		выбор заказчика	м	28,5	0,17	18,3 + 7,5 + 10 %
23	Труба PP-R, армированная стекловолокном, PN20 Ø20×2,8 (Т3)	ГОСТ 32415-2013		выбор заказчика	м	36	0,15	22,5 + 10,2 + 10 %
24	Труба канализационная ПП Ø40 (К1)	ГОСТ 32414-2013		выбор заказчика	м	1		0,1 + 0,6 + 10 %
25	Труба канализационная ПП Ø50 (К1)	ГОСТ 32414-2013		выбор заказчика	м	16		11,6 + 2,7 + 10 %
26	Труба канализационная ПП Ø110 (К1)	ГОСТ 32414-2013		выбор заказчика	м	8,5		6,7 + 0,7 + 10 %
	Фасонные части и выводы							
27	Отвод канализационный ПП 45° Ø50	ГОСТ 32414-2013		выбор заказчика	шт	18		2 шт. на поворот
28	Отвод канализационный ПП 45° Ø110	ГОСТ 32414-2013		выбор заказчика	шт	16		2 шт. на поворот
29	Тройник канализационный ПП 45° (врезки ветвей)	ГОСТ 32414-2013		выбор заказчика	шт	11		
30	Ревизия канализационная ПП (после поворота трассы)	ГОСТ 32414-2013		выбор заказчика	шт	9		доступ сохранить
31	Фитинги PP-R Ø20: тройники, угольники 90° (ветви и повороты В1, Т3)	ГОСТ 32415-2013		выбор заказчика	шт	51		
32	Водорозетка PP-R Ø20×½" настенная, с креплением	ГОСТ 32415-2013		выбор заказчика	шт	23		коды — лист выводов
	Узлы ввода, люки, короба							
33	Кран шаровой латунный Ду15 PN16 (отключение ввода)	аналог		выбор заказчика	шт	6		Ст В1-1, Ст Т3-1, Ст В1-2, Ст Т3-2, Ст В1-3, Ст Т3-3
34	Фильтр сетчатый косой Ду15	аналог		выбор заказчика	шт	6		
35	Счётчик воды крыльчатый Ду15 (ХВ, ГВ), с поверкой	аналог		выбор заказчика	шт	6		пломба УК
36	Клапан обратный Ду15	аналог		выбор заказчика	шт	6		
37	Люк ревизионный нажимной под плитку 300×400 мм	аналог		выбор заказчика	шт	3		к стоякам и арматуре
38	Звукоизоляция стояка К1 в коробе: рулонный звукоизоляционный материал ≥ 10 мм, обмотка стояка на высоту этажа	аналог		выбор заказчика	м	8,4		Ст К1-1, Ст К1-2 (кухня), Ст К1-3
39	Короб К1 над полом: профиль ПН/ПС, ГКЛВ 12,5 мм под плитку	аналог		выбор заказчика	м	11,6		сечение — лист разводки

Примечания

1. Форма 1 ГОСТ 21.110-2013, ширины граф изменены по п. 4.1. «Аналог» — аналог по характеристикам: модели внести до черновых работ, привязки выводов сверить по паспортам.
2. Бытовая техника не входит (показана арматура подключения), мойка — в комплекте кухни. Длины труб — трасса листа разводки + подъёмы + 10 %.
3. Стояк К1 в коробе — звукоизоляция стояка в коробе без жёсткого контакта короба с трубой.
4. Расчёт систем водоснабжения и канализации, диаметры магистралей и подбор оборудования выполняет проектная организация.

Допущения и предложения на листе

Основа листа: размеры и контуры этажей подобраны проектировщиком по составу помещений и площадям этажей с картинки 470 px (размеры на ней не читаются); обмер и исходный проект — задание (К-1); высоты: 1-й этаж 2800 мм, мансарда 2700 мм (горизонтальная часть) приняты; скаты кровли мансарды приняты по картинке: колено 1200 мм, уклон 45°, конёк вдоль длинной стороны; проект КР — задание (К-2); наружные стены 400 мм, перегородки 120 мм приняты (К-1); разрешённая мощность 15 кВт принята по типовым ТУ для частного дома (К-4); подрайон климата не задан — принят не северный (жилые от 2,5 м) (К-7).

См. лист открытых вопросов (лист 7, записи К-1, К-2, К-4, К-7).

Изм.	Кол.уч	Лист	№ док.	Подп.	Дата
Разраб.		Кырлан А.С.			21.10.26
Пров.					
ГИП					
Н. контр.					
Утв.					

ГД-2026-010-АИ

Дом 331 м²

Общая площадь 270,67* м² · * размеры приняты, не замерены (реестр — л. 7, К-1)

Дизайн-проект интерьера

Стадия	Лист	Листов
РП	53	159

Спецификация сантехнического оборудования

М б/м

Кырлан Александр Сергеевич

выпуск 18.10.2026 № 9365d64cec · стр. 57 из 197

Спецификация светильников и сценарии освещения

Светильники, ленты и блоки питания, слои света и сценарии по помещениям · б/м

Спецификация светильников

Поз.	Марки	Наименование	Установка	Кол.	P, Вт	Σ P, Вт	Ф, лм	Тц, К	Ra	Угол, °	IP	Дим.	Группа	Пом.
1	Св1–Св8, Св31–Св37	Встраиваемый точечный	в ГКЛ, корпус ≤ 70 мм	15	12	180	1000	3000	90	—	20	—	L1, L4	1, 5
2	Св38, Св39	Линейный светильник	на поверхности	1,2 м	8	16	700	3000	90	—	20	—	L5	1
3	Св40	Лента светодиодная 24 В	в коробе, профиль с рассеивателем	10,2 м	9,6/м	97,9	900/м	2700	90	—	20	да	L6	1
4	Св17–Св22	Встраиваемый точечный	в ГКЛ, корпус ≤ 70 мм	24	12	288	1050	2700	90	—	20	—	L7	2, 16, 18, 19
5	Св23	Лента светодиодная 24 В	в коробе, профиль с рассеивателем	5,4 м	9,6/м	51,8	900/м	2700	90	—	20	да	L8	2
6	Св10, Св11, Св24, Св25	Настенный (бра)	на стене, H=1500	10	6	60	400	2700	90	60	20	да	L3, L9	2, 13, 16, 18, 19
7	Св12–Св14, Св51	Встраиваемый точечный	в ГКЛ, корпус ≤ 70 мм	7	6	42	500	3000	90	—	44	—	L4, L17	3, 15, 20
8	Св15, Св52	Настенный светильник над зеркалом, драйвер встроен	над зеркалом, H=1900	3	8	24	600	3000	90	—	44	—	L5, L18	3, 15, 20
9	Св16, Св55, Св58	Потолочный накладной	на потолке	4	10	40	900	3000	90	—	20	—	L6, L19, L21	4, 7, 9, 14
10	Св9	Подвесной	подвес, низ H=1600	1	15	15	1200	2700	90	—	20	—	L2	5
11	Св10	Лента светодиодная 24 В	в карнизе короба, профиль с рассеивателем	21,1 м	9,6/м	202,9	900/м	2700	90	—	20	да	L3	5
12	Св26–Св29, Св53, Св54	Встраиваемый точечный	в ГКЛ, корпус ≤ 70 мм	8	7	56	600	3000	90	—	20	—	L10	6, 8, 17
13	Св30	Лента светодиодная 24 В	в коробе, профиль с рассеивателем, датчик движения	1,8 м	4,8/м	8,6	150/м	2700	90	—	20	нет	L11	8
14	Св56, Св57	Потолочный накладной	на потолке	2	24	48	2500	3000	90	—	20	—	L20	10
15	Св54	Встраиваемый точечный	встраиваемый	2	9	18	800	3000	90	—	44	—	L17	11, 12
16	Св1–Св8	Встраиваемый точечный	в ГКЛ, корпус ≤ 70 мм	8	12	96	1000	2700	90	—	20	—	L1	13
17	Св9, Св23	Лента светодиодная 24 В	в карнизе короба, профиль с рассеивателем	12 м	9,6/м	115,2	900/м	2700	90	—	20	да	L2, L8	13, 19
18	Св23	Лента светодиодная 24 В	в коробе, профиль с рассеивателем	3,2 м	9,6/м	30,7	900/м	2700	90	—	20	да	L8	16
19	Св23	Лента светодиодная 24 В	в карнизе короба, профиль с рассеивателем	15,5 м	9,6/м	149,2	900/м	2700	90	—	20	да	L8	18
20	Св50	Встраиваемый точечный	в ГКЛ, корпус ≤ 70 мм	1	7	7	600	3000	90	—	44	—	L17	20
		Итого		**85 шт + 70,5 м**		**1546,4**								

LED-ленты, линейные светильники и блоки питания

Марка	Пом.	L, м	U, В	Вт/м	Σ P, Вт	БП	P БП, Вт	Загр., %	Питание	Доступ к БП
Св38	1	0,6	24	—	8	БП2	30	53	встроенный ввод	в навесном модуле М26, съёмная панель
Св39	1	0,6	24	—	8	БП2	30	53	встроенный ввод	в навесном модуле М26, съёмная панель
Св40	1	10,2	24	9,6	97,9	БП3	150	65	с двух концов	люк 300×300 в нише фигуры потолка У2
Св23	2	5,4	24	9,6	51,8	БП4	200	26	с двух концов	люк 300×300 в нише фигуры потолка У2
Св10	5	21,1	24	9,6	202,9	БП1	300	68	с двух концов	люк 300×300 в коробе потолка У1
Св30	8	1,8	24	4,8	8,6	БП5	20	43	с одного конца	в шкафу М16, верхняя полка
Св9	13	6	24	9,6	57,6	БП6	200	29	с двух концов	люк 300×300 в коробе потолка У1
Св23	16	3,2	24	9,6	30,7	БП7	200	15	с двух концов	люк 300×300 в нише фигуры потолка У2
Св23	18	15,5	24	9,6	149,2	БП8	200	75	с двух концов	люк 300×300 в коробе потолка У1
Св23	19	6	24	9,6	57,6	БП9	200	29	с двух концов	люк 300×300 в коробе потолка У1

Сценарии освещения

Пом.	Сценарий	Группы и уровни, %	Чем включается
2	Вечер	L7 споты — 0; L8 подсветка короба — 100; L9 бра — 100	S4, S5, S6
5	Вечер	L1 общий свет (споты) — 0; L2 подвес над обеденным столом — 100; L3 лента в карнизе (диммер) — 50	S1, S2**, S2** светорегулятор, S3
5	Гости	L1 общий свет (споты) — 100; L2 подвес над обеденным столом — 100; L3 лента в карнизе (диммер) — 100	S1, S2**, S2** светорегулятор, S3
5	Кино	L1 общий свет (споты) — 0; L2 подвес над обеденным столом — 0; L3 лента в карнизе (диммер) — 20	S2**, S2** светорегулятор, S3
5	Уборка	L1 общий свет (споты) — 100; L2 подвес над обеденным столом — 100; L3 лента в карнизе (диммер) — 0	S1, S2**, S3
13	Вечер	L1 общий свет (споты) — 0; L2 подвес над обеденным столом — 100; L3 лента в карнизе (диммер) — 100	S1, S2**, S2** светорегулятор, S3
13	Уборка	L1 общий свет (споты) — 100; L2 подвес над обеденным столом — 100; L3 лента в карнизе (диммер) — 0	S1, S2**, S3
16	Вечер	L7 споты — 0; L8 подсветка короба — 100; L9 бра — 100	S4, S5, S6
18	Вечер	L7 споты — 0; L8 подсветка короба — 100; L9 бра — 100	S4, S5, S6
19	Вечер	L7 споты — 0; L8 подсветка короба — 100; L9 бра — 100	S4, S5, S6

Допущения и предложения на листе

Основа листа: размеры и контуры этажей подобраны проектировщиком по составу помещений и площадям этажей с картинки 470 px (размеры на ней не читаются); обмер и исходный проект — задание (К-1); высоты: 1-й этаж 2800 мм, мансарда 2700 мм (горизонтальная часть) приняты; скаты кровли мансарды приняты по картинке: колено 1200 мм, уклон 45°, конёк вдоль длинной стороны; проект КР — задание (К-2); наружные стены 400 мм, перегородки 120 мм приняты (К-1); разрешённая мощность 15 кВт принята по типовым ТУ для частного дома (К-4); подрайон климата не задан — принят не северный (жилые от 2,5 м) (К-7).

Знак «**» — предложение проектировщика, заказчиком не утверждено (согласовать с заказчиком): записи в реестре нет: S2 — светорегулятор добавлен под диммируемую ленту L3; уровни сценариев выбраны конвейером.

См. лист открытых вопросов (лист 7, записи К-1, К-2, К-4, К-7).

Примечания

1. Позиции и марки Св — те же, что на плане освещения (лист «План освещения») и в ведомости светильников (лист 37); группы L — по плану выключателей (лист «План выключателей»).
2. Модели светильников не назначены: подбор по графам спецификации — поток, Тц, Ra, угол, IP и диммирование не хуже указанных, мощность не больше; встраиваемые — под глубину короба (графа «Установка»). IP 20 — сухие помещения.
3. Длина LED-ленты в карнизе — по линии карниза плана потолков (лист «План потолков»); Σ P = Вт/м × длина. Блок питания загружен не больше чем на 80 %; лента 24 В длиннее 10 м питается с двух концов; доступ к блоку питания — люк ревизии 300×300 мм или место, указанное в таблице.
4. Сценарии: уровень — доля максимальной яркости группы, %; 0 — группа выключена. Уровень ниже 100 % — только у групп на светорегуляторе (задний фронт, ТЕ) с диммируемыми драйверами и блоками питания.
5. Мощность и поток — по паспортам принятых изделий, Σ P — установленная мощность освещения. Оценка освещённости — на плане освещения; это не светотехнический расчёт.
6. Не поместилось строк таблиц: 20 — продолжение выпустить отдельным листом.

Изм.	Кол.уч	Лист	№ док.	Подп.	Дата
Разраб.		Кырлан А.С.			21.10.26
Пров.					
ГИП					
Н. контр.					
Утв.					

ГД-2026-010-АИ

Дом 331 м²

Общая площадь 270,67* м² · * размеры приняты, не замерены (реестр — л. 7, К-1)

Дизайн-проект интерьера

Стадия	Лист	Листов
РП	54	159

Спецификация светильников и сценарии освещения
М б/м

Кырлан Александр Сергеевич

выпуск 18.10.2026 № 9365d64cec · стр. 58 из 197

План потолков · 1-й этаж

Уровни и марки потолков, короба с подсветкой, ниши под шторы, люки, вырезы · отметки низа от ±0,000 чистого пола · размеры в мм

ПРЕДВАРИТЕЛЬНО · не для производства работ · открыто пунктов: 6 (реестр — л. 7)

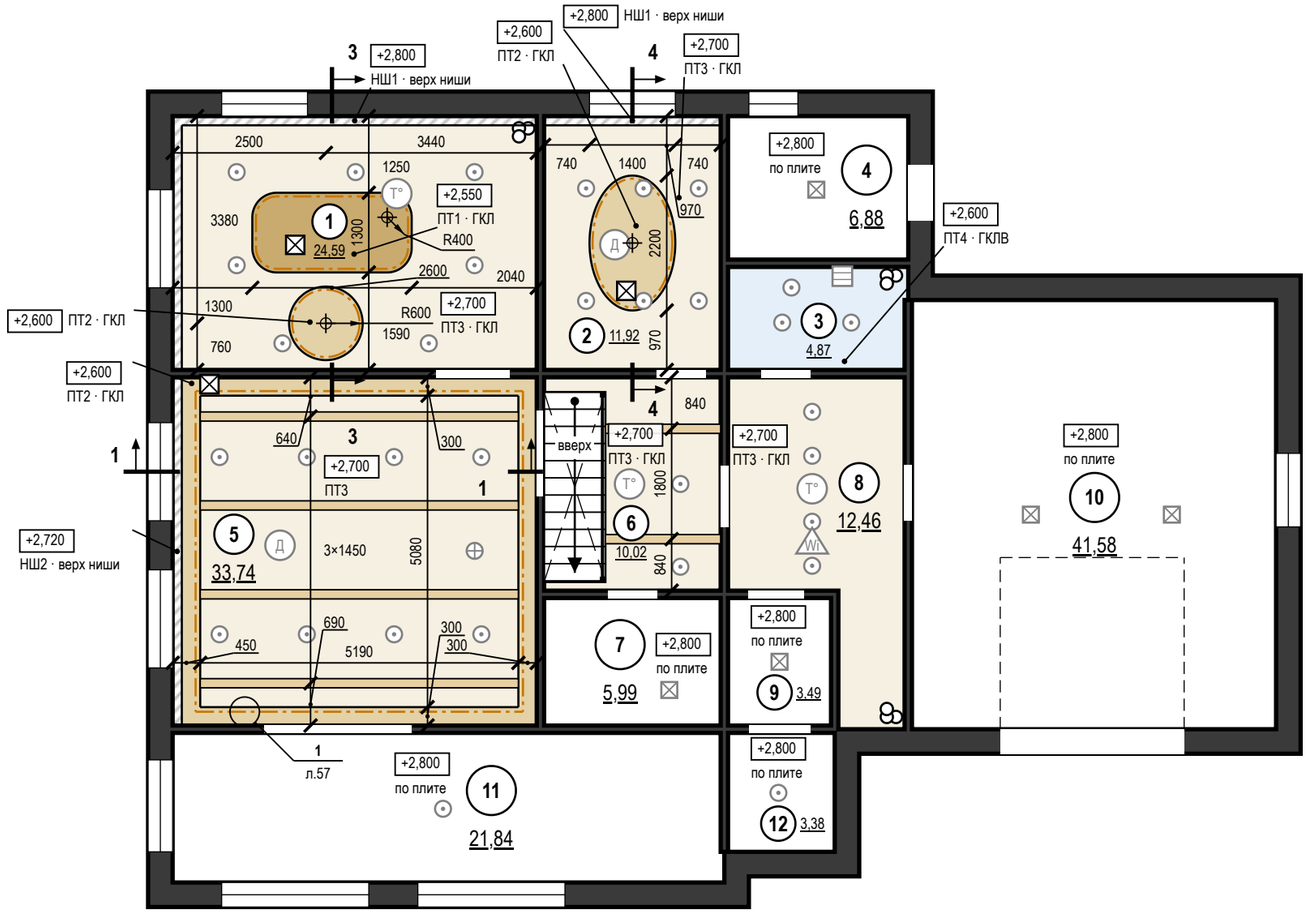

Условные обозначения

- ПТ1 — ГКЛ по каркасу П113, низ +2,550
- ПТ2 — ГКЛ по каркасу П113, низ +2,600
- ПТ3 — ГКЛ по каркасу П113, низ +2,700
- ПТ4 — ГКЛВ по каркасу П113, низ +2,600
- потолок по плите перекрытия (низ отметкой у помещения)
- НШ1 — ниша под шторы 150×100, верх +2,800
- НШ2 — ниша под шторы 150×120, верх +2,720
- граница уровней потолка (перепад)
- проём лестницы в перекрытии: потолка нет, по кромке — борт ГКЛ до плиты
- LED-лента в нише подсветки (карниз короба, ниша фигуры)
- стояк: К1 — канализация, В1 — ХВС, Т3 — ГВС
- балка декоративная 150×120 мм
- люк ревизии в потолке 300×300 мм (доступ к БП LED)

Ведомость потолков

Пом.	Марка	Конструкция	Низ / верх ниши	S, м²	Q
1	ПТ1	ГКЛ П113, остров + LED	+2,550	3,24	Q3
1	ПТ2	ГКЛ П113, круг + LED	+2,600	1,13	Q3
1	ПТ3	ГКЛ П113	+2,700	18,73	Q3
1	НШ1	ниша под шторы 150×100	+2,800	1,49	
2	ПТ2	ГКЛ П113, эллипс + LED	+2,600	2,42	Q3
2	ПТ3	ГКЛ П113	+2,700	9,07	Q3
2	НШ1	ниша под шторы 150×100	+2,800	0,43	
3	ПТ4	ГКЛВ П113	+2,600	4,87	Q3
4		по плите, окраска	+2,800	6,88	
5	ПТ2	ГКЛ П113, короб LED	+2,600	6,52	Q3
5	ПТ3	ГКЛ П113	+2,700	26,37	Q3
5	НШ2	ниша под шторы 150×120	+2,720	0,85	
6	ПТ3	ГКЛ П113	+2,700	6,92	Q3
7		по плите, окраска	+2,800	5,99	
8	ПТ3	ГКЛ П113	+2,700	12,46	Q3
9		по плите, окраска	+2,800	3,49	
10		по плите, окраска	+2,800	41,58	
11		по плите, окраска	+2,800	21,84	
12		по плите, окраска	+2,800	3,38	
		Итого		**177,66**	

Ведомость вырезов и закладных в потолке

Марка	Устройство	Кол.	Пом.
	Светильник встраиваемый (марки — план освещения)	32	1, 2, 3, 5, 6, 8, 11, 12
	Светильник накладной (марки — план освещения)	5	4, 7, 9, 10
	Светильник подвесной (марки — план освещения)	1	5
ИП2, ИП1	Извещатель дымовой	2	2, 5
ИП4, ИП6, ИП3	Извещатель тепловой	3	1, 6, 8
AP1**	Точка доступа Wi-Fi, PoE	1	8
ВР2	Решётка вытяжная (вентилятор)	1	3
	Люк ревизии 300×300	3	1, 2, 5

Условные обозначения (продолжение)

- светильник встраиваемый — подложка с плана освещения
- светильник накладной — подложка с плана освещения
- светильник подвесной — подложка с плана освещения
- извещатель дымовой на потолке — подложка
- извещатель тепловой на потолке — подложка
- точка доступа Wi-Fi на потолке — подложка
- решётка вытяжки в потолке — подложка с плана вентиляции
- линия разреза у стен помещения, стрелка — направление взгляда
- место узла: номер узла на полке, под полкой — лист
- +2,600 — отметка низа потолка, м (у ниши под шторы — верх ниши); под ней марка потолка
- 1 — номер помещения, площадь м²

Примечания

1. За отметку ±0,000 принят уровень чистого пола сухих помещений (готовое покрытие), а не существующего пола; пол пом. 3, 11, 12 — −0,015, −0,030; существующий пол снимается до плиты, его отметка не замерена. Отметки в прямоугольниках — низ потолка; низ плиты перекрытия +2,800. Марка потолка — одна конструкция и отметка на весь альбом.
2. Потолки ГКЛ — каркасная система П113: подвесы через 1000 (с запасом: СП 163, табл. 14 — до 1100 при 0,15 кН/м²), несущие профили через 500, основные через 1200 мм; листы — поперёк несущих профилей. В помещениях 3 — ГКЛВ на оцинкованном каркасе.
3. Нижний уровень — пояс-короб по периметру шириной 300 мм (карниз подсветки + 150 мм полки), верхний — поле внутри пояса: пом. 5.
4. LED-лента в алюминиевом профиле посередине карниза короба шириной 300 мм (узел 1, лист 57); длина по плану: пом. 5 — 21,1 м (в плане освещения 21,1).
5. Балки декоративные 150×120 мм, фальш-балка, массив лиственницы под маслом: пом. 5 — 4 шт., 20,8 м; пом. 6 — 2 шт., 3,8 м, низ +2,580; крепление — на закладной брус 50×50 к каркасу П113, саморезы скрыто.
6. Ниши под шторы 150×100 мм — на всю длину стены с окном; карниз — на закладной до обшивки (узел 2 — пом. 1, 2, лист 57; узел 4 — пом. 5, лист 58).
7. Примыкание к стенам: теневой шов 15 мм, техзазор 3 мм — пом. 2, 5, по стенам, выровненным штукатуркой (узел 1); пом. 1, 3, 6, 8 — разделительная лента.
8. Светильники и потолочные устройства — подложка с планов освещения, слаботочных систем и вентиляции (положение — по ним); вырезы и закладные — по ведомости на листе, до обшивки; отверстия не совмещать с профилями, глубина корпуса светильника до 70 мм.
9. Разрезы 1–1 — лист 57; 3–3, 4–4 — лист 58; высоты мебели и дверных блоков сверены с низом потолка в разрезах; гибка бортов фигур и ленты ниш — там же; размеры фигурных уровней фрагменты 1, 2 (лист 60).
10. Узлы по выноскам на плане: узлы 1, 2 — лист 57; узлы 3, 4 — лист 58; узел 6 — лист 60.
11. Шпаклевание ГКЛ и условия приёмки — Q3: рассеянный дневной свет, осмотр с 2 м; боковой свет не оценивается.
12. Люки ревизии 300×300 мм — по центру блоков питания LED (БП3, БП4, БП1; координаты — план освещения).
13. Пом. 6: над маршем лестницы Л-1* — проём перекрытия 1000×3100 мм; потолок ГКЛ по кромке проёма закрыт бортом до плиты (ГКЛ по ПН 28×27, длина кромки 5,1 м); светильники и устройства в проёме не ставятся.
14. Пом. 4, 7, 9, 10, 11, 12 — потолок по плите без подвесной системы; отделка — по ведомости отделки.

1000 мм · печать 1:1

Допущения и предложения на листе. Знак «*» принято (замерить). Знак «**» предложено (согласовать). См. лист открытых вопросов (лист 7).

Изм.	Кол.уч	Лист	№ док.	Подп.	Дата
Разраб.		Кырлан А.С.			21.10.26
Пров.					
ГИП					
Н. контр.					
Утв.					

ГД-2026-010-АИ

Дом 331 м²

Общая площадь 270,67* м² · * размеры приняты, не замерены (реестр — л. 7, К-1)

Дизайн-проект интерьера

Стадия	Лист	Листов
РП	55	159

План потолков · 1-й этаж

М 1:100

Кырлан Александр Сергеевич

выпуск 18.10.2026 № 9365d64cec · стр. 59 из 197

План потолков · Мансарда

Уровни и марки потолков, короба с подсветкой, ниши под шторы, люки, вырезы · отметки низа от ±0,000 чистого пола · размеры в мм

ПРЕДВАРИТЕЛЬНО · не для производства работ · открыто пунктов: 6 (реестр — л. 7)

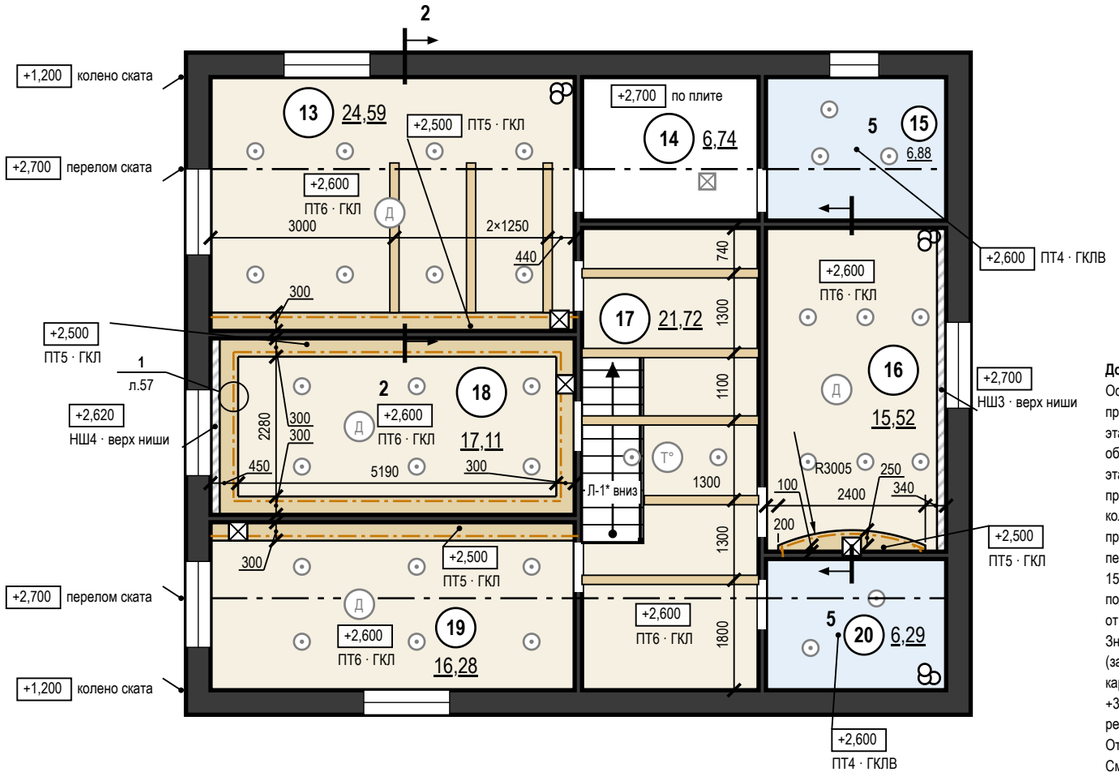

Допущения и предложения на листе

Основа листа: размеры и контуры этажей подобраны проектировщиком по составу помещений и площадям этажей с картинки 470 px (размеры на ней не читаются); обмер и исходный проект — задание (К-1); высоты: 1-й этаж 2800 мм, мансарда 2700 мм (горизонтальная часть) приняты; скаты кровли мансарды приняты по картинке: колено 1200 мм, уклон 45°, конёк вдоль длинной стороны; проект КР — задание (К-2); наружные стены 400 мм, перегородки 120 мм приняты (К-1); разрешённая мощность 15 кВт принята по типовым ТУ для частного дома (К-4); подрайон климата не задан — принят не северный (жилые от 2,5 м) (К-7).

Знак «*» — принято, не замерено и не подтверждено (замерить на объекте): К-6: Л-1 — габарит марша снят с картинки заказчика (11 проступей в холле 3,6 м), а до отм. +3,150 нужно 18 подъёмов — одномаршевая не встаёт: решение по К-6.

Открытые вопросы и конфликты по листу: К-2, К-7.

См. лист открытых вопросов (лист 7, записи К-1, К-2, К-4, К-6, К-7).

Ведомость потолков

Пом.	Марка	Конструкция	Низ / верх ниши	S, м²	Q
13	ПТ5	ГКЛ П113, короб LED	+2,500	1,78	Q3
13	ПТ6	ГКЛ П113	+2,600	22,81	Q3
14		по плите, окраска	+2,700	6,74	
15	ПТ4	ГКЛВ П113	+2,600	6,88	Q3
16	ПТ5	ГКЛ П113, дуга + LED	+2,500	0,64	Q3
16	ПТ6	ГКЛ П113	+2,600	14,09	Q3
16	НШ3	ниша под шторы 150×100	+2,700	0,79	
17	ПТ6	ГКЛ П113	+2,600	21,72	Q3
18	ПТ5	ГКЛ П113, короб LED	+2,500	4,84	Q3
18	ПТ6	ГКЛ П113	+2,600	11,84	Q3
18	НШ4	ниша под шторы 150×120	+2,620	0,43	
19	ПТ5	ГКЛ П113, короб LED	+2,500	1,78	Q3
19	ПТ6	ГКЛ П113	+2,600	14,50	Q3
20	ПТ4	ГКЛВ П113	+2,600	6,29	Q3
		Итого		**115,13**	

Ведомость вырезов и закладных в потолке

Марка	Устройство	Кол.	Пом.
	Светильник встраиваемый (марки — план освещения)	33	13, 15, 16, 17, 18, 19, 20
	Светильник накладной (марки — план освещения)	1	14
ИП1, ИП2, ИП2, ИП2	Извещатель дымовой	4	13, 16, 18, 19
ИП6	Извещатель тепловой	1	17
	Люк ревизии 300×300	4	13, 16, 18, 19

Условные обозначения (продолжение)

- линия перелома потолка мансарды: скат → горизонтальная часть; отметки ската у плана
- стояк: К1 — канализация, В1 — ХВС, Т3 — ГВС
- балка декоративная 150×120 мм
- люк ревизии в потолке 300×300 мм (доступ к БП LED)
- светильник встраиваемый — подложка с плана освещения
- светильник накладной — подложка с плана освещения
- Д — извещатель дымовой на потолке — подложка
- Т° — извещатель тепловой на потолке — подложка
- линия разреза у стен помещения, стрелка — направление взгляда
- место узла: номер узла на полке, под полкой — лист
- +2,600 — отметка низа потолка, м (у ниши под шторы — верх ниши); под ней марка потолка
- 1 — номер помещения, площадь м²

Условные обозначения

- ПТ4 — ГКЛВ по каркасу П113, низ +2,600
- ПТ5 — ГКЛ по каркасу П113, низ +2,500, пояс-короб с карнизом LED
- ПТ6 — ГКЛ по каркасу П113, низ +2,600
- потолок по плите перекрытия (низ — отметкой у помещения)
- НШ3 — ниша под шторы 150×100, верх +2,700
- НШ4 — ниша под шторы 150×120, верх +2,620
- граница уровней потолка (перепад)
- LED-лента в нише подсветки (карниз короба, ниша фигуры)

Примечания

1. За отметку ±0,000 принят уровень чистого пола сухих помещений (готовое покрытие), а не существующего пола; пол пом. 15, 20 — −0,015; верх плиты перекрытия −0,064 — расчётный по пирогу пола, не замерен; существующий пол снимается до плиты, его отметка не замерена. Отметки в прямоугольниках — низ потолка; низ плиты перекрытия +2,700. Марка потолка — одна конструкция и отметка на весь альбом.
2. Мансарда: потолок по скатам кровли — от +1,200 у наружных стен вдоль конька до +2,700 у линий перелома (штрихпунктир), между ними — горизонтальная часть +2,700 (в пом. 13, 15, 16, 17, 18, 19, 20 горизонтальная часть подшита ниже — по марке и отметке потолка; скат обшит до линии подшивки); над слуховыми окнами скат поднят до горизонтальной части. Обшивка скатов — по стропилам с пароизоляцией по проекту КР.
3. Потолки ГКЛ — каркасная система П113: подвесы через 1000 (с запасом: СП 163, табл. 14 — до 1100 при 0,15 кН/м²), несущие профили через 500, основные через 1200 мм; листы — поперёк несущих профилей. В помещениях 15, 20 — ГКЛВ на оцинкованном каркасе.
4. Нижний уровень — пояс-короб по периметру шириной 300 мм (карниз подсветки + 150 мм полки), верхний — поле внутри пояса: пом. 18.
5. Короб-полоса у одной стены (не по периметру): ПТ5 шириной 300 мм — пом. 13 у стены В, пом. 19 у стены А.
6. LED-лента в алюминиевом профиле посередине карниза короба шириной 300 мм (узел 1, лист 57); длина по плану: пом. 13 — 6,0 м (в плане освещения 6); пом. 18 — 15,5 м (в плане освещения 15,5); пом. 19 — 6,0 м (в плане освещения 6).
7. Балки декоративные 150×120 мм, фальш-балка, массив лиственницы под маслом: пом. 13 — 3 шт., 7,3 м; пом. 17 — 5 шт., 14,4 м, низ +2,480; крепление — на закладной брус 50×50 к каркасу П113, саморезы скрыто.
8. Ниши под шторы 150×100 мм — на всю длину стены с окном; карниз — на закладной до обшивки (узел 2 — пом. 16, лист 57; узел 4 — пом. 18, лист 58).
9. Примыкание к стенам: теневой шов 15 мм, техзазор 3 мм — пом. 16, 18, по стенам, выровненным штукатуркой (узел 1); пом. 13, 15, 17, 19, 20 — разделительная лента.
10. Светильники и потолочные устройства — подложка с планов освещения, слаботочных систем и вентиляции (положение — по ним); вырезы и закладные — по ведомости на листе, до обшивки; отверстия не совмещать с профилями, глубина корпуса светильника до 70 мм.
11. Разрезы 2–2 — лист 57; 5–5 — лист 59; высоты мебели и дверных блоков сверены с низом потолка в разрезах; гибка бортов фигур и ленты ниш — там же; размеры фигурных уровней — фрагмент 3 (лист 60).
12. Узлы по выноскам на плане: узлы 1, 2 — лист 57; узел 4 — лист 58; узел 5 — лист 59.
13. Шпаклевание ГКЛ и условия приёмки — Q3: рассеянный дневной свет, осмотр с 2 м; боковой свет не оценивается.
14. Люки ревизии 300×300 мм — по центру блоков питания LED (БП6, БП7, БП8, БП9; координаты — план освещения).
15. Пом. 14 — потолок по плите без подвесной системы; отделка — по ведомости отделки.

1000 мм · печать 1:1

Изм.	Кол.уч	Лист	№ док.	Подп.	Дата
Разраб.		Кырлан А.С.			21.10.26
Пров.					
ГИП					
Н. контр.					
Утв.					

ГД-2026-010-АИ

Дом 331 м²

Общая площадь 270,67* м² · * размеры приняты, не замерены (реестр — л. 7, К-1)

Дизайн-проект интерьера

Стадия	Лист	Листов
РП	56	159

План потолков · Мансарда

М 1:100

Кырлан Александр Сергеевич

выпуск 18.10.2026 № 9365d64cec · стр. 60 из 197

Разрезы и узлы потолков

Разрезы по потолкам с отметками уровней · узлы коробов и ниш · размеры в мм

Разрез 1–1 (М 1:40)

Пом. 5 Гостиная

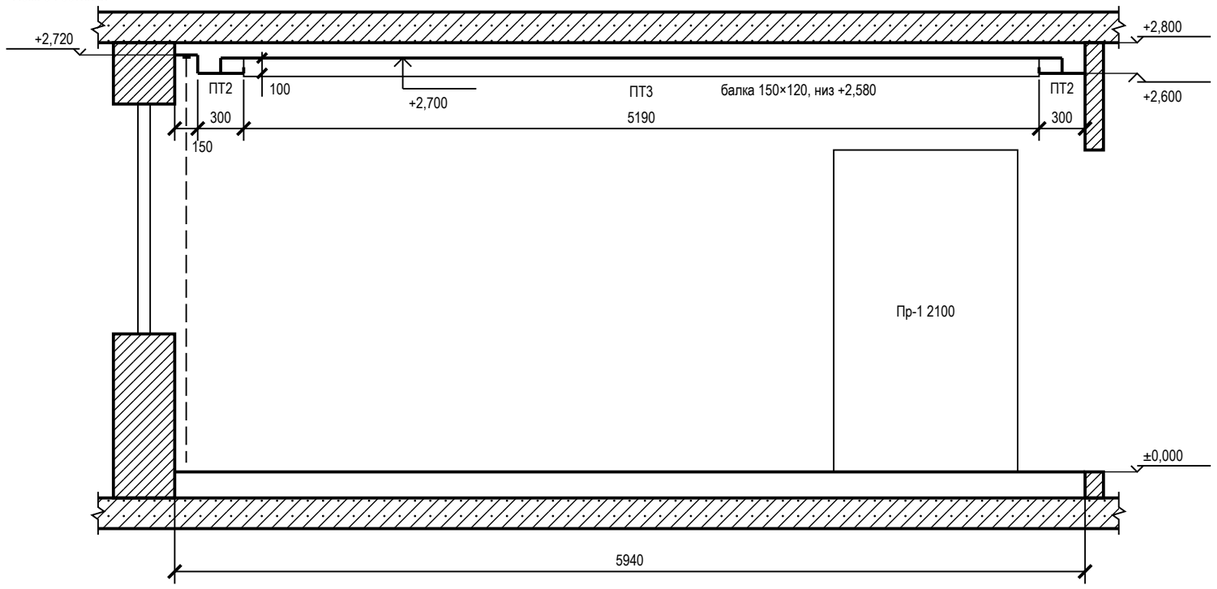

Разрез 2–2 (М 1:40)

Пом. 13 Спальня мастер (мансарда, потолок по скату)

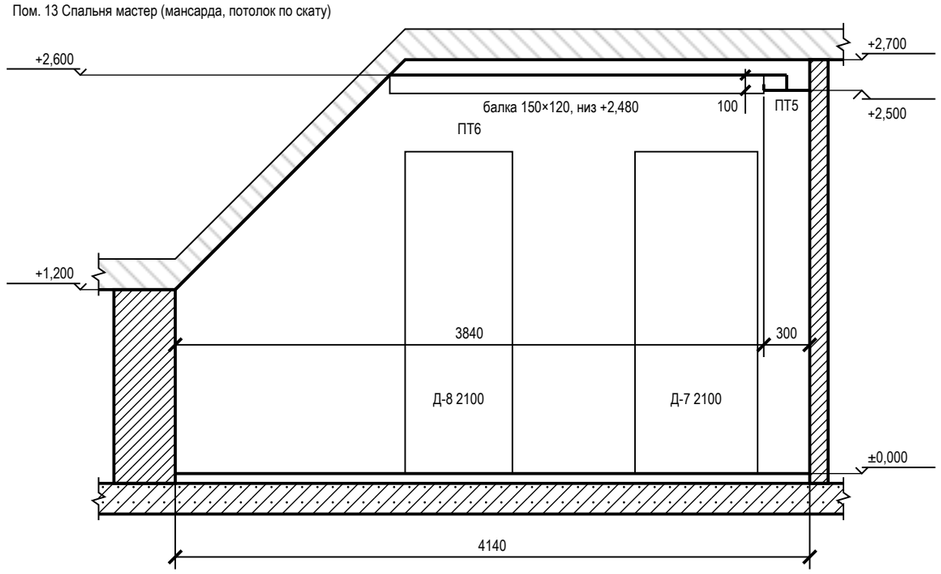

1 Короб с LED-подсветкой, теневой шов (М 1:10)

Пом. 5, 13, 18, 19; карниз 150×100, щель под свет 60 мм

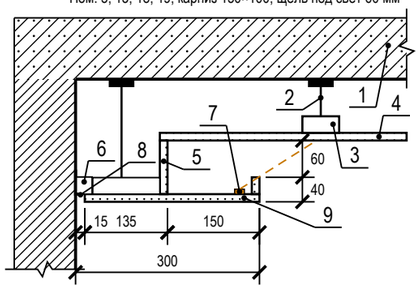

1 — плита перекрытия
2 — подвес прямой, шаг 1000 мм
3 — ПП 60×27: несущие через 500, основные через 1200 мм
4 — ГКЛ 12,5 по П113 — верхний уровень
5 — задняя стенка и бортик карниза — ГКЛ 12,5
6 — ПН 28×27 по периметру, к стене через 500 мм
7 — LED-лента в алюминиевом профиле
8 — теневой профиль: шов 15 мм, зазор 3 мм — пом. 5, 18; пом. 13, 19 — разделительная лента
9 — низ короба — ГКЛ 12,5 по ПП 60×27

Отметки по помещениям, м

Пом.	низ короба	верх. уровень	низ плиты
5	+2,600	+2,700	+2,800
13, 18, 19	+2,500	+2,600	+2,700

2 Ниша под шторы (М 1:10)

Пом. 1, 2, 16; без подсветки; закладные под карниз — до обшивки

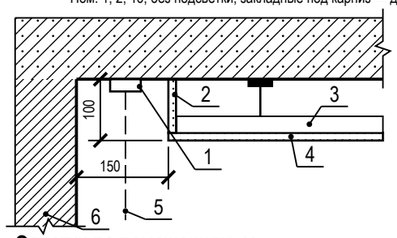

1 — карниз (шина), высота с верхом портьеры 100 мм
2 — стенка ниши — ГКЛ 12,5
3 — ПП 60×27 — каркас короба
4 — низ короба нижнего уровня — ГКЛ 12,5
5 — портьера
6 — стена с окном

Отметки по помещениям, м

Пом.	низ потолка	верх ниши	низ плиты
1, 2	+2,700	+2,800	+2,800
16	+2,600	+2,700	+2,700

Условные обозначения

- плита перекрытия в сечении
- стена в сечении
- потолок ГКЛ в сечении; под линией — марка потолка (план потолков)
- мебель и дверные проёмы за секущей плоскостью; число — марка и верх от чистого пола, мм
- портьера в нише под шторы
- балка декоративная: в сечении — заливка, за плоскостью — тонкой линией; низ балки — подписью у балки или отметкой справа
- кровля над мансардой (условно, по проекту КР)

Допущения и предложения на листе

Основа листа: размеры и контуры этажей подобраны проектировщиком по составу помещений и площадям этажей с картинки 470 px (размеры на ней не читаются); обмер и исходный проект — задание (К-1); высоты: 1-й этаж 2800 мм, мансарда 2700 мм (горизонтальная часть) приняты; скаты кровли мансарды приняты по картинке: колено 1200 мм, уклон 45°, конёк вдоль длинной стороны; проект КР — задание (К-2); наружные стены 400 мм, перегородки 120 мм приняты (К-1); разрешённая мощность 15 кВт принята по типовым ТУ для частного дома (К-4); подрайон климата не задан — принят не северный (жилые от 2,5 м) (К-7).
См. лист открытых вопросов (лист 7, записи К-1, К-2, К-4, К-7).

Примечания

1. Разрезы — по линиям 1–1, 2–2 на плане потолков. Отметки — от ±0,000 чистого пола, м; размеры — мм.
2. Высоты мебели и дверных блоков за секущей плоскостью сверены с низом потолка над ними: верх ниже низа короба и поля.
3. ГКЛ 12,5 мм по каркасу П113; перепад уровней и бортик карниза — ГКЛ по ПП 60×27 (узел 1 — на этом листе). Ниша под шторы — на всю длину стены с окном, карниз на закладной до обшивки (узел 2 — на этом листе; узел 4 — лист 58).
4. Толщины плит перекрытия и пирога пола показаны условно.
5. Ведомость объёмов потолков (лист ГКЛ, профиль, подвесы, лента, блоки питания, люки) — на листе 59.
6. Фрагменты 1, 3, 2 — помещения с фигурными уровнями (размеры фигур, радиусы, отметки) — на листе 60.

1000 мм · печать 1:1

Изм.	Кол.уч	Лист	№ док.	Подп.	Дата
Разраб.		Кырлан А.С.			21.10.26
Пров.					
ГИП					
Н. контр.					
Утв.					

ГД-2026-010-АИ

Дом 331 м²

Общая площадь 270,67* м² · * размеры приняты, не замерены (реестр — л. 7, К-1)

Дизайн-проект интерьера

Стадия	Лист	Листов
РП	57	159

Разрезы и узлы потолков

М 1:40; 1:10

Кырлан Александр Сергеевич

выпуск 18.10.2026 № 9365d64cec · стр. 61 из 197

Разрезы и узлы потолков (продолжение)

Разрезы по потолкам с отметками уровней · узлы коробов и ниш · размеры в мм

Разрез 3–3 (М 1:40)

Пом. 1 Кухня-столовая

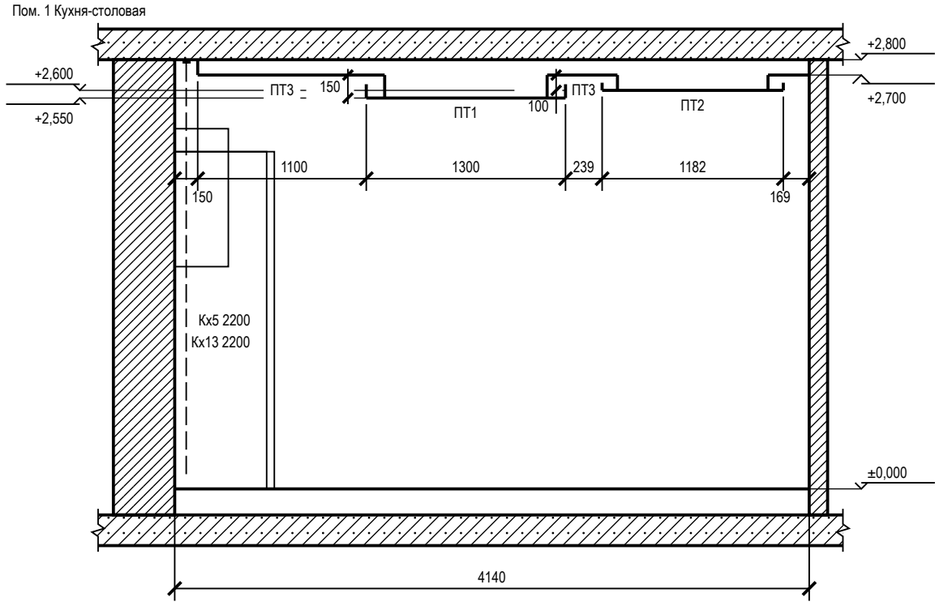

Разрез 4–4 (М 1:40)

Пом. 2 Кабинет-гостевая

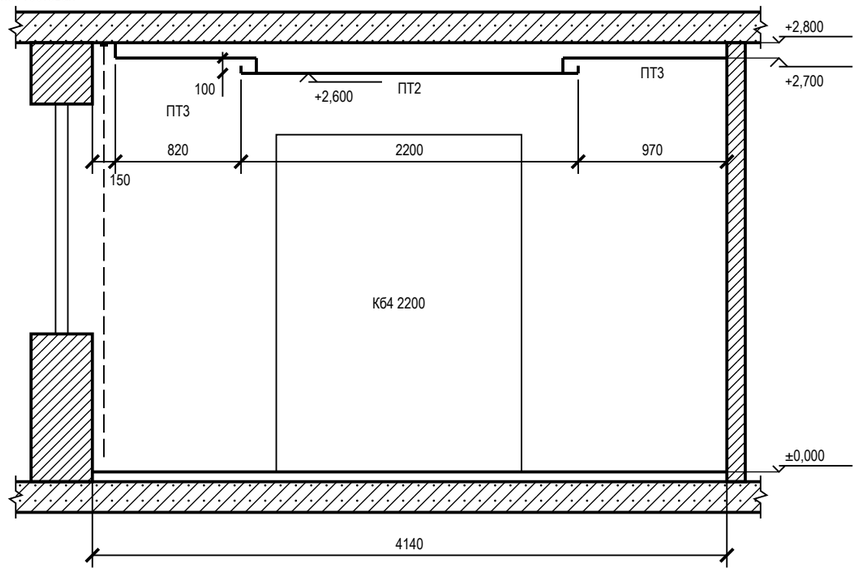

3 Ниша LED фигурного уровня (М 1:10)

Пом. 1; карниз 120×100, щель под свет 60 мм

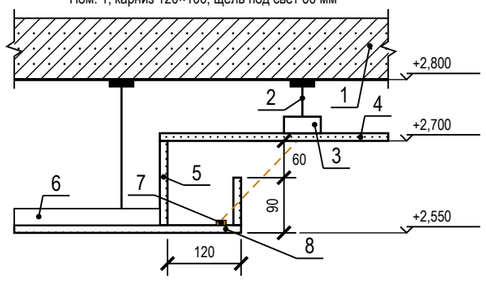

1 — плита перекрытия
2 — подвес прямой, шаг 1000 мм
3 — ПП 60×27: несущие через 500, основные через 1200 мм
4 — ГКЛ 12,5 по П113 — верхний уровень
5 — задняя стенка и бортик карниза — ГКЛ 12,5
6 — ПП 60×27 каркаса нижнего уровня, ПН по контуру фигуры (на дуге — с надрезами)
7 — LED-лента в алюминиевом профиле
8 — низ короба — ГКЛ 12,5 по ПП 60×27

4 Ниша под шторы (М 1:10)

Пом. 5, 18; без подсветки; закладные под карниз — до обшивки

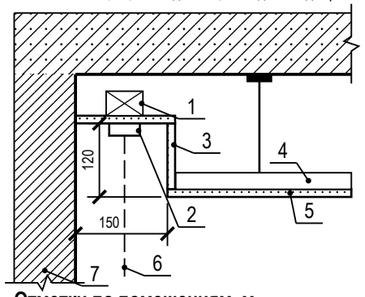

1 — закладная под карниз — брус 40×50
2 — карниз (шина), высота с верхом портьеры 100 мм
3 — стенка и потолок ниши — ГКЛ 12,5
4 — ПП 60×27 — каркас короба
5 — низ короба нижнего уровня — ГКЛ 12,5
6 — портьера
7 — стена с окном

Отметки по помещениям, м

Пом.	низ потолка	верх ниши	низ плиты
5	+2,600	+2,720	+2,800
18	+2,500	+2,620	+2,700

Условные обозначения

- плита перекрытия в сечении
- стена в сечении
- потолок ГКЛ в сечении; под линией — марка потолка (план потолков)
- мебель и дверные проёмы за секущей плоскостью; число марка и верх от чистого пола, мм
- портьера в нише под шторы
- LED-лента в нише подсветки (карниз короба, ниша фигуры)

Примечания

1. Разрезы — по линиям 3–3, 4–4 на плане потолков. Отметки — от ±0,000 чистого пола, м; размеры — мм.
2. Высоты мебели и дверных блоков за секущей плоскостью сверены с низом потолка над ними: верх ниже низа короба и поля.
3. ГКЛ 12,5 мм по каркасу П113; узлы коробов и ниш под шторы: узел 1 — лист 57; узел 2 — лист 57; узел 4 — на этом листе.
4. Толщины плит перекрытия и пирога пола показаны условно.

Допущения и предложения на листе

Основа листа: размеры и контуры этажей подобраны проектировщиком по составу помещений и площадям этажей с картинки 470 px (размеры на ней не читаются); обмер и исходный проект — задание (К-1); высоты: 1-й этаж 2800 мм, мансарда 2700 мм (горизонтальная часть) приняты; скаты кровли мансарды приняты по картинке: колено 1200 мм, уклон 45°, конёк вдоль длинной стороны; проект КР — задание (К-2); наружные стены 400 мм, перегородки 120 мм приняты (К-1); разрешённая мощность 15 кВт принята по типовым ТУ для частного дома (К-4); подрайон климата не задан — принят не северный (жилые от 2,5 м) (К-7).
См. лист открытых вопросов (лист 7, записи К-1, К-2, К-4, К-7).

1000 мм · печать 1:1

Изм.	Кол.уч	Лист	№ док.	Подп.	Дата
Разраб.		Кырлан А.С.			21.10.26
Пров.					
ГИП					
Н. контр.					
Утв.					

ГД-2026-010-АИ

Дом 331 м²

Общая площадь 270,67* м² · * размеры приняты, не замерены (реестр — л. 7, К-1)

Дизайн-проект интерьера	Стадия	Лист	Листов
	РП	58	159

Разрезы и узлы потолков (продолжение)

М 1:40; 1:10

Кырлан Александр Сергеевич

выпуск 18.10.2026 № 9365d64cec · стр. 62 из 197

Разрезы и узлы потолков (продолжение)

Разрезы по потолкам с отметками уровней · узлы коробов и ниш · ведомость объёмов · размеры в мм

ПРЕДВАРИТЕЛЬНО · не для производства работ · открыто пунктов: 6 (реестр — л. 7)

Разрез 5–5 (М 1:25)

Пом. 16 Спальня 2 (мансарда, разрез по горизонтальной части)

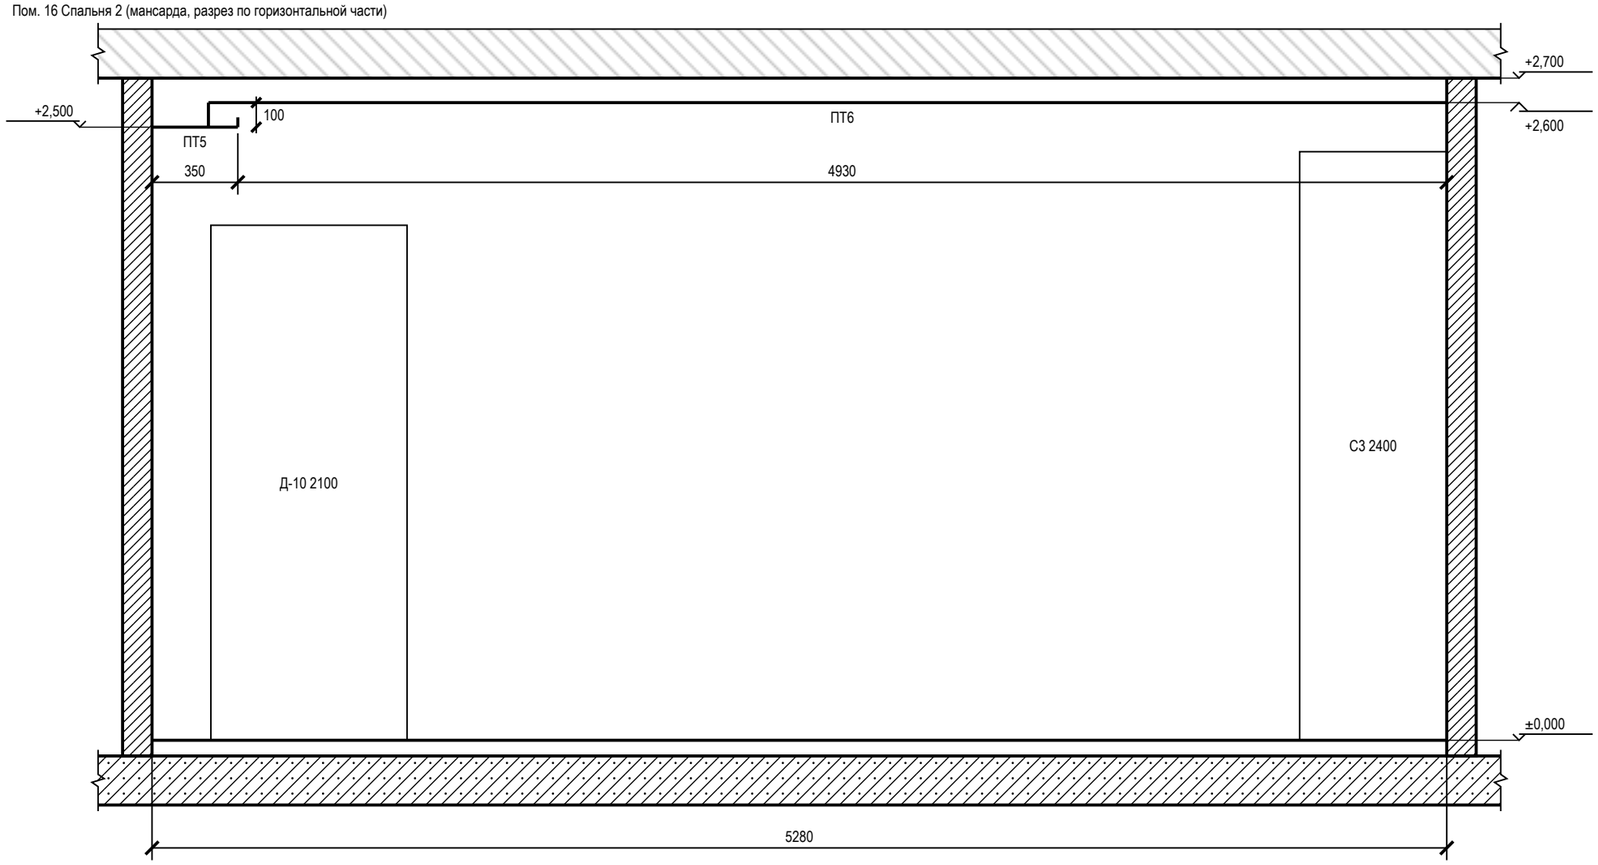

5 Ниша LED фигурного уровня (М 1:10)

Пом. 16; карниз 120×100, щель под свет 60 мм

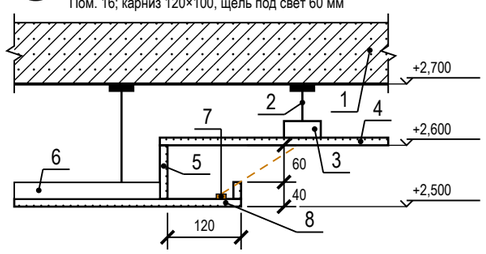

1 — плита перекрытия
2 — подвес прямой, шаг 1000 мм
3 — ПП 60×27: несущие через 500, основные через 1200 мм
4 — ГКЛ 12,5 по П113 — верхний уровень
5 — задняя стенка и бортик карниза — ГКЛ 12,5
6 — ПП 60×27 каркаса нижнего уровня, ПН по контуру фигуры (на дуге — с надрезами)
7 — LED-лента в алюминиевом профиле
8 — низ короба — ГКЛ 12,5 по ПП 60×27

Условные обозначения

- плита перекрытия в сечении
- стена в сечении
- потолок ГКЛ в сечении; под линией — марка потолка (план потолков)
- мебель и дверные проёмы за секущей плоскостью; число марка и верх от чистого пола, мм
- кровля над мансардой (условно, по проекту КР)
- LED-лента в нише подсветки (карниз короба, ниша фигуры)

Ведомость объёмов потолков

Позиция	Ед.	Кол.	Пом.
Лист ГКЛ 12,5	м²	205,77	1, 2, 5, 6, 8, 13, 16, 17, 18, 19
Лист ГКЛВ 12,5	м²	18,04	3, 15, 20
Лист ГКЛ арочный 6,5	м²	4,06	1, 2
Борта и карнизы (входят в площади листов выше)	м²	22,93	1, 2, 5, 6, 13, 16, 18, 19
Профиль ПП 60×27	м	601,81	1, 2, 3, 5, 6, 8, 13, 15, 16, 17, 18, 19, 20
Профиль ПН 28×27	м	474,23	1, 2, 3, 5, 6, 8, 13, 15, 16, 17, 18, 19, 20
Подвес прямой	шт.	226	1, 2, 3, 5, 6, 8, 13, 15, 16, 17, 18, 19, 20
Анкер-клин к плите	шт.	226	1, 2, 3, 5, 6, 8, 13, 15, 16, 17, 18, 19, 20
Шуруп TN 3,5×25	шт.	5194	1, 2, 3, 5, 6, 8, 13, 15, 16, 17, 18, 19, 20
Лента армирующая для швов	м	271,01	1, 2, 3, 5, 6, 8, 13, 15, 16, 17, 18, 19, 20
Шпаклёвка для швов	кг	90,34	1, 2, 3, 5, 6, 8, 13, 15, 16, 17, 18, 19, 20
Грунтовка (швы)	л	22,58	1, 2, 3, 5, 6, 8, 13, 15, 16, 17, 18, 19, 20
Лента разделительная по периметру	м	209,80	1, 2, 3, 5, 6, 8, 13, 15, 16, 17, 18, 19, 20
Сплошная шпаклёвка и окраска (площадь развёртки)	м²	225,84	1, 2, 3, 5, 6, 8, 13, 15, 16, 17, 18, 19, 20
Лента LED	м	67,45	1, 2, 5, 13, 16, 18, 19
Требуемая мощность блоков питания	Вт	842	1, 2, 5, 13, 16, 18, 19
Установленная мощность блоков питания	Вт	1450	1, 2, 5, 13, 16, 18, 19
Блок питания LED	шт.	7	1, 2, 5, 13, 16, 18, 19
Люк ревизии	шт.	7	1, 2, 5, 13, 16, 18, 19

Допущения и предложения на листе

Основа листа: размеры и контуры этажей подобраны проектировщиком по составу помещений и площадям этажей с картинки 470 px (размеры на ней не читаются); обмер и исходный проект — задание (К-1); высоты: 1-й этаж 2800 мм, мансарда 2700 мм (горизонтальная часть) приняты; скаты кровли мансарды приняты по картинке: колено 1200 мм, уклон 45°, конёк вдоль длинной стороны; проект КР — задание (К-2); наружные стены 400 мм, перегородки 120 мм приняты (К-1); разрешённая мощность 15 кВт принята по типовым ТУ для частного дома (К-4); подрайон климата не задан — принят не северный (жилые от 2,5 м) (К-7).

См. лист открытых вопросов (лист 7, записи К-1, К-2, К-4, К-7).

Примечания

1. Разрезы — по линиям 5–5 на плане потолков. Отметки — от ±0,000 чистого пола, м; размеры — мм.
2. Высоты мебели и дверных блоков за секущей плоскостью сверены с низом потолка над ними: верх ниже низа короба и поля.
3. ГКЛ 12,5 мм по каркасу П113; узлы коробов и ниш под шторы: узел 1 — лист 57; узел 2 — лист 57; узел 4 — лист 58.
4. Толщины плит перекрытия и пирога пола показаны условно.
5. Ведомость объёмов — по геометрии плана потолков: Лист ГКЛ 12,5 — плоскости уровней + борта (без арочных участков); Лист ГКЛВ 12,5 — плоскости уровней + борта; Лист ГКЛ арочный 6,5 — кривая борта × высота борта и стенки ниши × 2 слоя (R400 мокрая гибка, R600 мокрая гибка, R445 мокрая гибка); Борта и карнизы — длина перепада × перепад; Профиль ПП 60×27 — S × (1/шаг несущ. + 1/шаг осн.) + стойки бортов; Профиль ПН 28×27 — периметр стен + 2 × перепады + карнизы; Подвес прямой — по раскладке: S уровня / (шаг осн. × шаг подвесов), пояс уже шага — ряд вдоль пояса, фигура — по контуру; шаг подвесов — не больше табл. 14 СП 163; Анкер-клин к плите — по одному на подвес (Knauf П113); Шуруп TN 3,5×25 — 23 шт./м² (Knauf П113, табл. 2 альбома П 11); Лента армирующая для швов — 1,2 м/м² листа (Knauf); Шпаклёвка для швов — 0,4 кг/м² листа, только швы (Knauf); Грунтовка (швы) — 0,1 л/м² листа, только швы (Knauf); Лента разделительная по периметру — периметр стен под потолком ГКЛ; Сплошная шпаклёвка и окраска (площадь развёртки) — плоскости + борта; расход — по паспорту материала (норма на сплошной слой не подтверждена, knowledge/ceilings.md 2.3); Лента LED — по оси карниза и ниши фигуры (план потолков); Требуемая мощность блоков питания — Вт/м × длина × 1,3; Установленная мощность блоков питания сумма мощностей блоков по плану освещения; Блок питания LED — блоки потолочных лент по плану освещения (БП3, БП4, БП1, БП6, БП7, БП8, БП9); Люк ревизии — план потолков; без запаса на подрезку (при закупке листа: ×1,075 при S > 20 м², ×1,175 — 10–20 м², ×1,275 — < 10 м²).

1000 мм · печать 1:1

Изм.	Кол.уч	Лист	№ док.	Подп.	Дата
Разраб.		Кырлан А.С.			21.10.26
Пров.					
ГИП					
Н. контр.					
Утв.					

ГД-2026-010-АИ

Дом 331 м²

Общая площадь 270,67* м² · * размеры приняты, не замерены (реестр — л. 7, К-1)

Дизайн-проект интерьера

Стадия	Лист	Листов
РП	59	159

Разрезы и узлы потолков (продолжение)

М 1:25; 1:10

Кырлан Александр Сергеевич

выпуск 18.10.2026 № 9365d64cec · стр. 63 из 197

Разрезы и узлы потолков (продолжение)

Узлы коробов и ниш · фрагменты фигурных уровней · размеры в мм

Фрагмент 1. Пом. 1 Кухня-столовая — уровни потолка (М 1:50)

Цепочки — от чистых граней стен; отметки — низ уровня от ±0,000

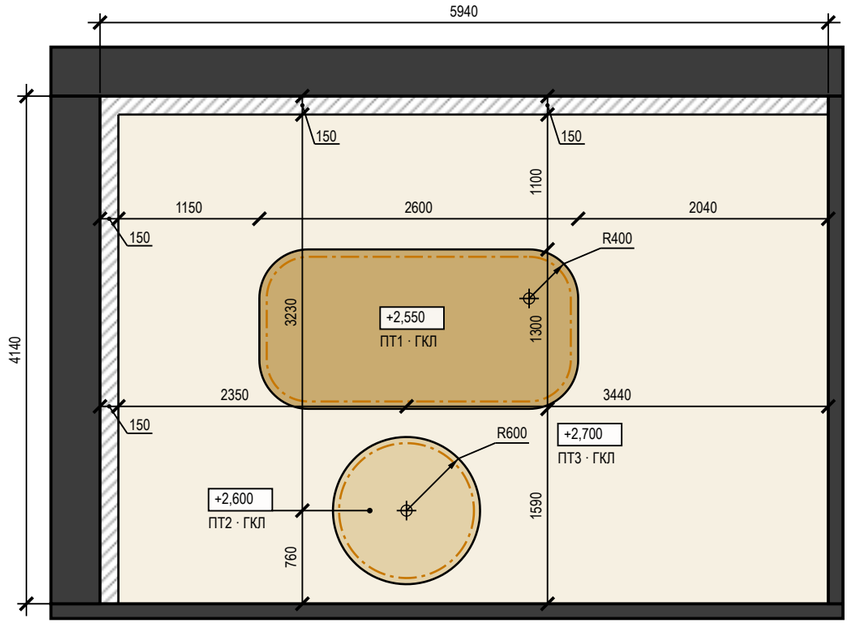

Фрагмент 3. Пом. 16 Спальня 2 — уровни потолка (М 1:50)

Цепочки — от чистых граней стен; отметки — низ уровня от ±0,000

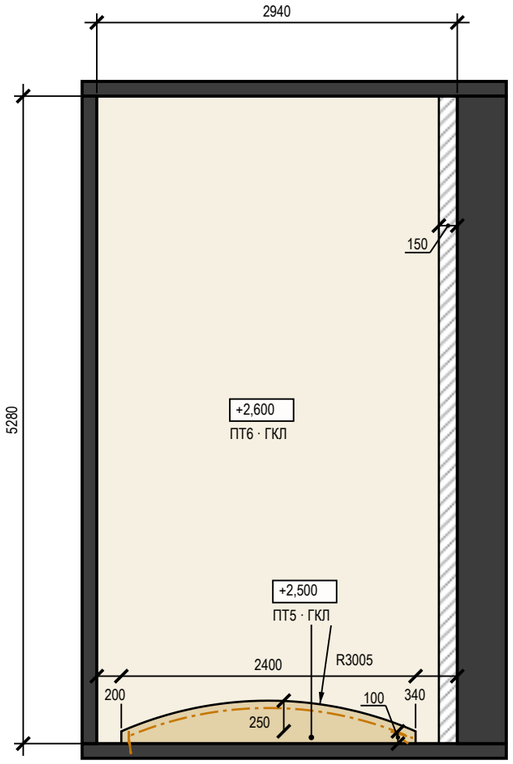

Фрагмент 2. Пом. 2 Кабинет-гостевая — уровни потолка (М 1:50)

Цепочки — от чистых граней стен; отметки — низ уровня от ±0,000

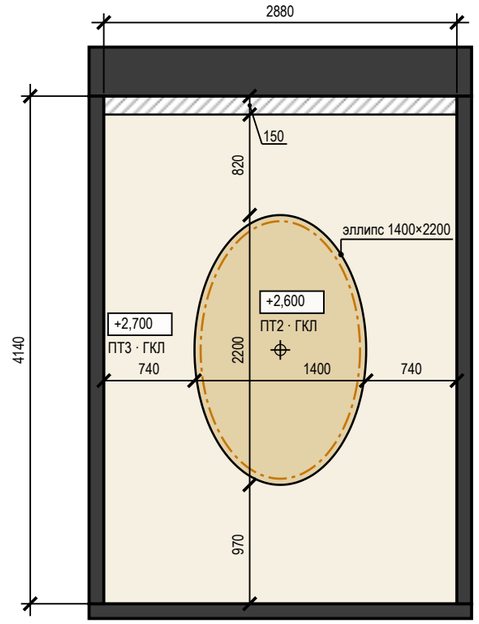

ПТ1 — низ +2,550 · ПТ2 — низ +2,600 · ПТ3 — низ +2,700
LED-лента в нише подсветки (карниз короба, ниша фигуры) · ниша под шторы

ПТ5 — низ +2,500 · ПТ6 — низ +2,600
LED-лента в нише подсветки (карниз короба, ниша фигуры) · ниша под шторы

ПТ2 — низ +2,600 · ПТ3 — низ +2,700
LED-лента в нише подсветки (карниз короба, ниша фигуры) · ниша под шторы

6 Ниша LED фигурного уровня (М 1:10)

Пом. 2; карниз 100×100, щель под свет 50 мм

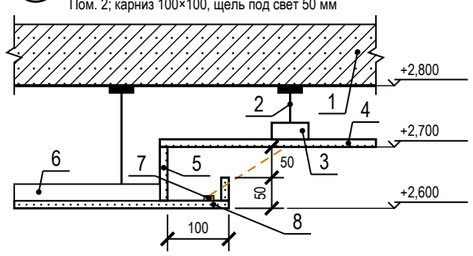

1 — плита перекрытия
2 — подвес прямой, шаг 1000 мм
3 — ПП 60×27: несущие через 500, основные через 1200 мм
4 — ГКЛ 12,5 по П113 — верхний уровень
5 — задняя стенка и бортик карниза — ГКЛ 12,5
6 — ПП 60×27 каркаса нижнего уровня, ПН по контуру фигуры (на дуге — с надрезами)
7 — LED-лента в алюминиевом профиле
8 — низ короба — ГКЛ 12,5 по ПП 60×27

Допущения и предложения на листе

Основа листа: размеры и контуры этажей подобраны проектировщиком по составу помещений и площадям этажей с картинки 470 px (размеры на ней не читаются); обмер и исходный проект — задание (К-1); высоты: 1-й этаж 2800 мм, мансарда 2700 мм (горизонтальная часть) приняты; скаты кровли мансарды приняты по картинке: колено 1200 мм, уклон 45°, конёк вдоль длинной стороны; проект КР — задание (К-2); наружные стены 400 мм, перегородки 120 мм приняты (К-1); разрешённая мощность 15 кВт принята по типовым ТУ для частного дома (К-4); подрайон климата не задан — принят не северный (жилые от 2,5 м) (К-7).
См. лист открытых вопросов (лист 7, записи К-1, К-2, К-4, К-7).

Примечания

1. ГКЛ 12,5 мм по каркасу П113; узлы коробов и ниш под шторы: узел 1 — лист 57; узел 2 — лист 57; узел 4 — лист 58; условные обозначения разрезов — на листе 57.
2. Фрагменты 1, 3, 2 — фигурные уровни потолка крупно: привязки краёв и центров фигур к чистым граням стен, радиусы (R) с центрами, хорда и стрелка дуги, отметки низа каждого уровня; цвета уровней — как на плане потолков.
3. Фигурные уровни: борт — ГКЛ по ПН с надрезами (на дуге шаг стоек борта 300 мм при R до 2500, 400 — до 5000) или по гнутому заводскому профилю (СП 163, 6.3.3); гибка: остров пом. 1 R400 — ГКЛ 6,5 мокрой гибкой; круг пом. 1 R600 — ГКЛ 6,5 мокрой гибкой; эллипс пом. 2 R445 — ГКЛ 6,5 мокрой гибкой; дуга пом. 16 R3005 — ГКЛ 12,5 сухой гибкой (СП 163, табл. 9). Лента в нише фигуры по оси: остров пом. 1 — 6,7 м, круг пом. 1 — 3,5 м, эллипс пом. 2 — 5,4 м, дуга пом. 16 — 3,2 м; узел ниши LED фигуры: узел 3 — лист 58 — пом. 1; узел 6 — на этом листе — пом. 2; узел 5 — лист 59 — пом. 16.

1000 мм · печать 1:1

Изм.	Кол.уч	Лист	№ док.	Подп.	Дата
Разраб.		Кырлан А.С.			21.10.26
Пров.					
ГИП					
Н. контр.					
Утв.					

ГД-2026-010-АИ

Дом 331 м²

Общая площадь 270,67* м² · * размеры приняты, не замерены (реестр — л. 7, К-1)

Дизайн-проект интерьера

Стадия	Лист	Листов
РП	60	159

Разрезы и узлы потолков (продолжение)

М 1:50; 1:10

Кырлан Александр Сергеевич

выпуск 18.10.2026 № 9365d64cec · стр. 64 из 197

Раскладка плитки. Планы полов

Раскладка от чистовых размеров · размеры в мм · отметки от ±0,000

Фрагмент 1. Санузел 1 этажа (пом. 3). Пол 600×600, шов 2 мм, М 1:50

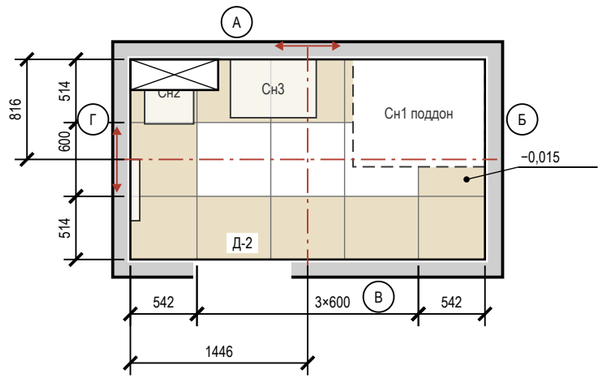

Фрагмент 2. Санузел мастер (пом. 15). Пол 600×600, шов 2 мм, М 1:50

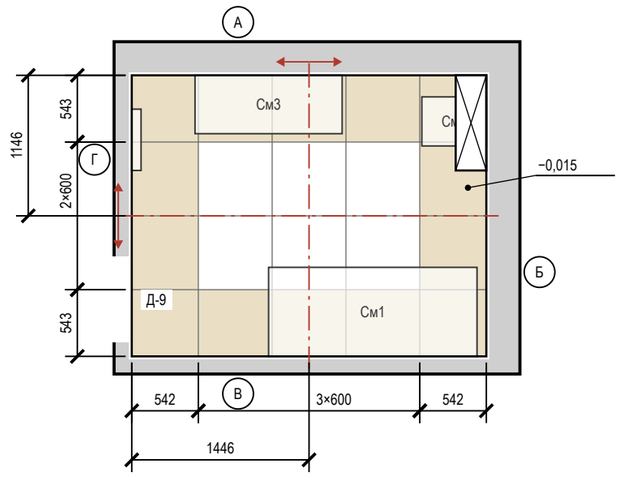

Фрагмент 3. Санузел 2 (пом. 20). Пол 600×600, шов 2 мм, М 1:50

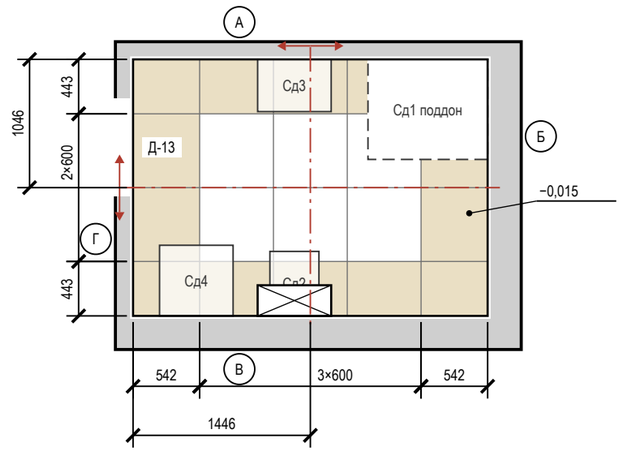

Ведомость материалов

Материал	Класс, код	Норма расхода	Кол-во
Затирка	CG2WA Mapei Ultracolor Plus 132	(a+b)/ab·шов·t·1,6	6,9 кг
Затирка	CG2WA	(a+b)/ab·шов·t·1,6	3,8 кг
Клей	C2 TE S1 Ceresit CM 17	1,5 кг/м²·мм, слой 5	682 кг (28 меш.)
Клей	C2 TE S1	1,5 кг/м²·мм, слой 5	370 кг (15 меш.)
Гидроизоляция	обмазочная, 2 слоя: пол, стены по периметру и зоны замачивания	по ТУ	43,1 м²
Демпф. лента	по периметру пола из плитки		85,5 м

Ведомость плитки

Помещение, поверхность	Плитка, код	Формат	Шов	S, м²	Целых	Подр.	С запасом
Санузел 1 этажа, пол	аналог: керамогранит под травертин	600×600	2	4,87	2	12	16
Санузел 1 этажа, стены А–Г	аналог: керамогранит под травертин	600×1200	2	19,67	11	19	34
Санузел 1 этажа, короб инсталляции	аналог: керамогранит под травертин	600×1200	2	1,64	0	6	7
Санузел мастер, пол	аналог: керамогранит под травертин	600×600	2	6,88	6	14	22
Санузел мастер, стены А–Г	аналог: керамогранит под травертин	600×1200	2	19,01	14	21	39
Санузел мастер, короб инсталляции	аналог: керамогранит под травертин	600×1200	2	1,73	0	6	7
Санузел 2, пол	аналог: керамогранит под травертин	600×600	2	6,29	5	14	21
Санузел 2, стены А–Г	аналог: керамогранит под травертин	600×1200	2	17,04	14	21	39
Санузел 2, короб инсталляции	аналог: керамогранит под травертин	600×1200	2	1,47	1	3	5
Котельная, пол	A8UZ	600×1200	2	6,88	0	10	11
Прихожая, пол	A8UZ	600×1200	2	12,46	3	12	17
Тамбур, пол	A8UZ	600×1200	2	3,49	0	6	7
Веранда, пол	A8UZ	600×1200	2	21,84	13	32	50
Крыльцо, пол	A8UZ	600×1200	2	3,38	0	6	7
Итого 600×600				18,04	13	40	59
Итого 600×1200				**108,60**	**56**	**142**	**223**

Условные обозначения

- плитка целая; тонкая линия — шов
- плитка с подрезкой (размер — на цепочке)
- ось старта; стрелки — направление укладки
- сантехприбор: габарит, высота по практике
- поддон душа — плитку пола под ним не кладут
- короб инсталляции: плитка пола — до короба
- отметка чистого пола на полке выноски, м
- (А) обозначение стены А–Г (как на развёртках)

Примечания

1. Раскладка от чистовых размеров: стены санузлов теряют 10 + 5 + 9 = 24 мм на сторону (штукатурка, клей, плитка); подрезки — чистые, без шва.
2. Старт — от центра помещения (штрихпунктир, стрелки — направление укладки); размер старта — от чистовых стен Г и А.
3. Раскладка пола «Котельная» и пола «Прихожая» и пола «Тамбур» и пола «Веранда» и пола «Крыльцо» — на листе «Раскладка плитки. Котельная. Прихожая. Тамбур. Веранда. Крыльцо».
4. Калибр партии не задан — до укладки замерить (рабочий размер W, ГОСТ 13996-2019) и пересчитать подрезки.
5. Количество: целые по раскладке + по одной на подрезку, запас 10 %; один артикул — одна партия и тон. Исключены поддон, короб, проёмы и места за коробом; S — по чистым граням: стены нетто = зона облицовки по ведомости отделки − место за коробом инсталляции 2,51 м² (плитку за коробом не кладут), короб — отдельной строкой.
6. Клей C2 TE S1 Ceresit CM 17; C2 TE S1 (ГОСТ Р 56387-2018), затирка CG2WA Mapei Ultracolor Plus 132; CG2WA; расход — по ТУ выбранной марки.
7. Гидроизоляция: пол и стены 200 мм от ЧП; у душа — до 2000 и 500 мм за поддон, над ванной — до 2000 и 300 мм за борт (см. развёртки); акт скрытых работ, пролив 24 ч.
8. Швы пола совмещены со швами стены А; по периметру — демпферная лента.
9. Отметка чистого пола −0,015, порог 15 мм; стык с соседним покрытием — по оси полотна двери.

Допущения и предложения на листе

Основа листа: размеры и контуры этажей подобраны проектировщиком по составу помещений и площадям этажей с картинки 470 px (размеры на ней не читаются); обмер и исходный проект — задание (К-1); высоты: 1-й этаж 2800 мм, мансарда 2700 мм (горизонтальная часть) приняты; скаты кровли мансарды приняты по картинке: колено 1200 мм, уклон 45°, конёк вдоль длинной стороны; проект КР — задание (К-2); наружные стены 400 мм, перегородки 120 мм приняты (К-1); разрешённая мощность 15 кВт принята по типовым ТУ для частного дома (К-4); подрайон климата не задан — принят не северный (жилые от 2,5 м) (К-7).
См. лист открытых вопросов (лист 7, записи К-1, К-2, К-4, К-7).

1000 мм · печать 1:1

Изм.	Кол.уч	Лист	№ док.	Подп.	Дата
Разраб.		Кырлан А.С.			21.10.26
Пров.					
ГИП					
Н. контр.					
Утв.					

ГД-2026-010-АИ

Дом 331 м²

Общая площадь 270,67* м² · * размеры приняты, не замерены (реестр — л. 7, К-1)

Дизайн-проект интерьера

Стадия	Лист	Листов
РП	61	159

Раскладка плитки. Планы полов

М 1:50

Кырлан Александр Сергеевич

выпуск 18.10.2026 № 9365d64cec · стр. 65 из 197

Раскладка плитки. Котельная. Прихожая. Тамбур. Веранда

Раскладка от чистовых размеров · размеры в мм · высоты фартука от чистого пола

ПРЕДВАРИТЕЛЬНО · не для производства работ · открыто пунктов: 6 (реестр — л. 7)

Фрагмент 1. Котельная (пом. 4). Пол 600×1200, шов 2 мм, М 1:50

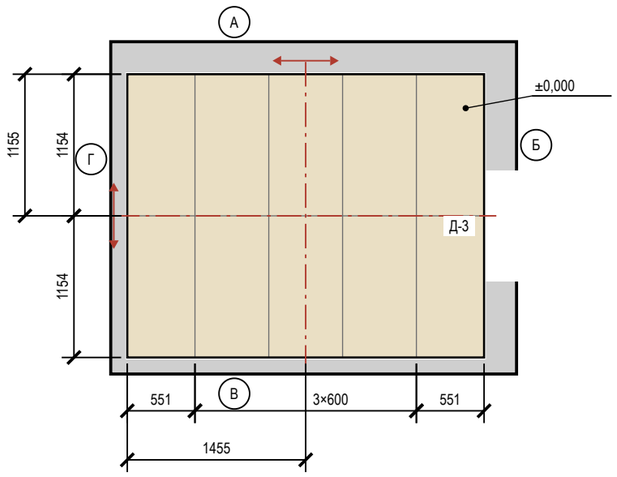

Фрагмент 2. Прихожая (пом. 8). Пол 600×1200, шов 2 мм, М 1:50

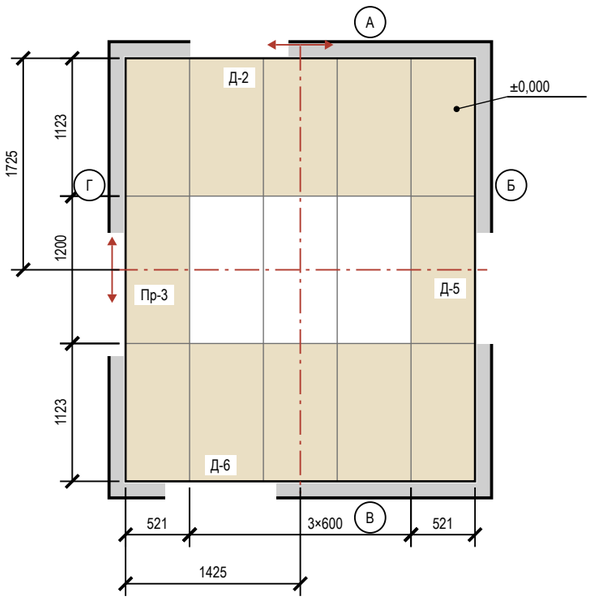

Фрагмент 3. Тамбур (пом. 9). Пол 600×1200, шов 2 мм, М 1:50

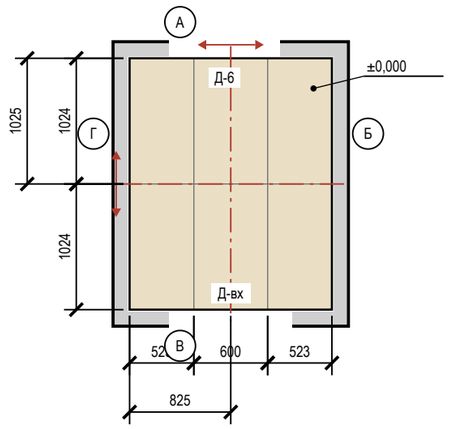

Условные обозначения

- плитка целая; тонкая линия — шов
- плитка с подрезкой (размер — на цепочке)
- ось старта; стрелки — направление укладки
- отметка чистого пола на полке выноски, м
- А — обозначение стены А–Г (как на развёртках)

Фрагмент 4. Веранда (пом. 11). Пол 600×1200, шов 2 мм, М 1:50

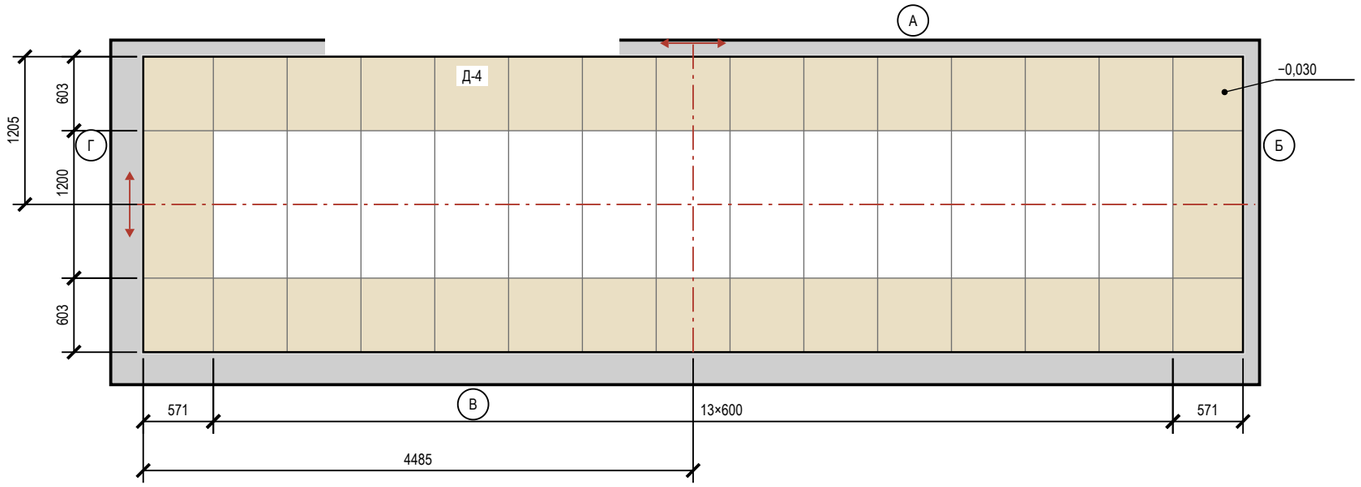

Примечания

1. Котельная: керамогранит 600×1200, длинная сторона — вдоль стен Б и Г, шов 2 мм, прямая раскладка от центра. Стены окрашены: раскладка от чистового контура минус штукатурка и шпаклёвка 15 мм на сторону (принято); подрезки 551 / 1154 мм, срез — под плинтус.
2. Котельная: деформационный зазор по периметру 8–10 мм под плинтусом; в проёмах — стык с соседним покрытием по оси полотна двери. Клей C2 TE S1, затирка CG2WA.
3. Прихожая: керамогранит 600×1200, длинная сторона — вдоль стен Б и Г, шов 2 мм, прямая раскладка от центра. Стены окрашены: раскладка от чистового контура минус штукатурка и шпаклёвка 15 мм на сторону (принято); подрезки 521 / 1123 мм, срез — под плинтус.
4. Прихожая: деформационный зазор по периметру 8–10 мм под плинтусом; в проёмах — стык с соседним покрытием по оси полотна двери. Клей C2 TE S1, затирка CG2WA.
5. Тамбур: керамогранит 600×1200, длинная сторона — вдоль стен Б и Г, шов 2 мм, прямая раскладка от центра. Стены окрашены: раскладка от чистового контура минус штукатурка и шпаклёвка 15 мм на сторону (принято); подрезки 523 / 1024 мм, срез — под плинтус.
6. Тамбур: деформационный зазор по периметру 8–10 мм под плинтусом; в проёмах — стык с соседним покрытием по оси полотна двери. Клей C2 TE S1, затирка CG2WA.
7. Веранда: керамогранит 600×1200, длинная сторона — вдоль стен Б и Г, шов 2 мм, прямая раскладка от центра. Стены окрашены: раскладка от чистового контура минус штукатурка и шпаклёвка 15 мм на сторону (принято); подрезки 571 / 603 мм, срез — под плинтус.
8. Веранда: деформационный зазор по периметру 8–10 мм под плинтусом; в проёмах — стык с соседним покрытием по оси полотна двери. Клей C2 TE S1, затирка CG2WA.
9. Клей, затирка и итог по форматам — в ведомостях листа «Раскладка плитки. Планы полов».

Подсчёт плитки

Поверхность	Формат	S, м²	Целых	Подр.	С запасом
Котельная, пол	600×1200	6,88	0	10	11
Прихожая, пол	600×1200	12,46	3	12	17
Тамбур, пол	600×1200	3,49	0	6	7
Веранда, пол	600×1200	21,84	13	32	50

1000 мм · печать 1:1

Допущения и предложения на листе

Основа листа: размеры и контуры этажей подобраны проектировщиком по составу помещений и площадям этажей с картинки 470 px (размеры на ней не читаются); обмер и исходный проект — задание (К-1); высоты: 1-й этаж 2800 мм, мансарда 2700 мм (горизонтальная часть) приняты; скаты кровли мансарды приняты по картинке: колено 1200 мм, уклон 45°, конёк вдоль длинной стороны; проект КР — задание (К-2); наружные стены 400 мм, перегородки 120 мм приняты (К-1); разрешённая мощность 15 кВт принята по типовым ТУ для частного дома (К-4); подрайон климата не задан — принят не северный (жилые от 2,5 м) (К-7).

Знак «**» — предложение проектировщика, заказчиком не утверждено (согласовать с заказчиком): записи в реестре нет: плинтус пом. 4, 8, 9, 11 — артикул изделия не выбран: позиция описана характеристиками («аналог по характеристикам»), артикул выбирается при закупке.

См. лист открытых вопросов (лист 7, записи К-1, К-2, К-4, К-7).

Изм.	Кол.уч	Лист	№ док.	Подп.	Дата
Разраб.		Кырлан А.С.			21.10.26
Пров.					
ГИП					
Н. контр.					
Утв.					

ГД-2026-010-АИ

Дом 331 м²

Общая площадь 270,67* м² · * размеры приняты, не замерены (реестр — л. 7, К-1)

Дизайн-проект интерьера	Стадия	Лист	Листов
	РП	62	159

Раскладка плитки. Котельная. Прихожая. Тамбур. Веранда

М 1:50

Кырлан Александр Сергеевич

выпуск 18.10.2026 № 9365d64cec · стр. 66 из 197

Раскладка плитки. Крыльцо

Раскладка от чистовых размеров · размеры в мм · высоты фартука от чистого пола

Фрагмент 1. Крыльцо (пом. 12). Пол 600×1200, шов 2 мм, М 1:20

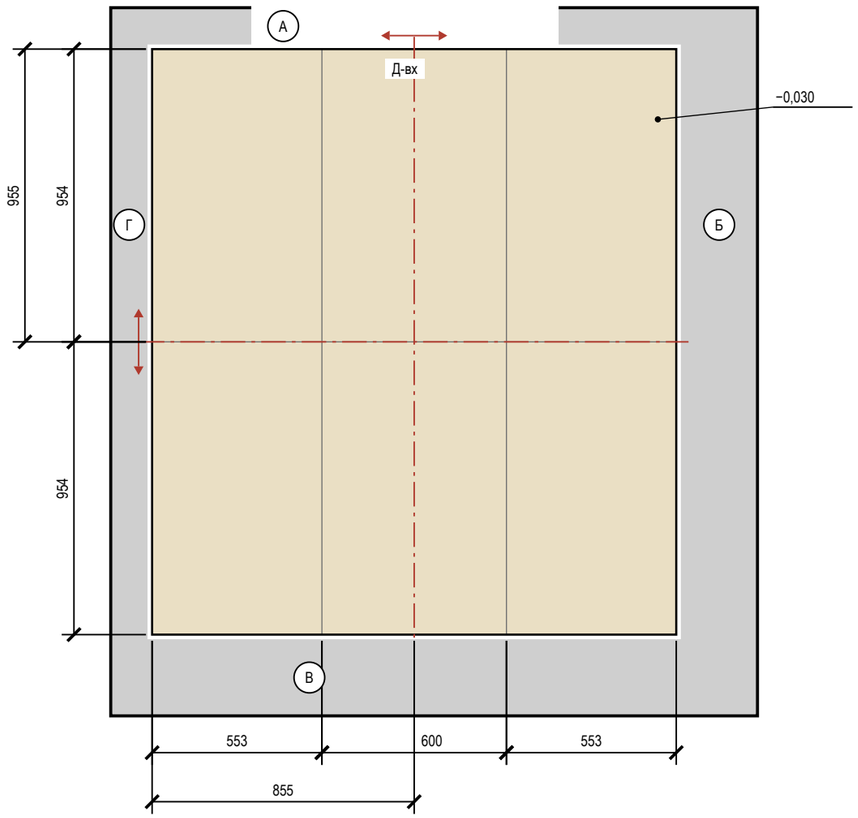

Условные обозначения

- плитка целая; тонкая линия — шов
- плитка с подрезкой (размер — на цепочке)
- ось старта; стрелки — направление укладки
- отметка чистого пола на полке выноски, м
- (А) обозначение стены А–Г (как на развёртках)

Подсчёт плитки

Поверхность	Формат	S, м²	Целых	Подр.	С запасом
Крыльцо, пол	600×1200	3,38	0	6	7

Примечания

1. Крыльцо: керамогранит 600×1200, длинная сторона — вдоль стен Б и Г, шов 2 мм, прямая раскладка от центра. Стены окрашены: раскладка от чистового контура минус штукатурка и шпаклёвка 15 мм на сторону (принято); подрезки 553 / 954 мм, срез — под плинтус.
2. Крыльцо: деформационный зазор по периметру 8–10 мм под плинтусом; в проёмах — стык с соседним покрытием по оси полотна двери. Клей C2 TE S1, затирка CG2WA.
3. Клей, затирка и итог по форматам — в ведомостях листа «Раскладка плитки. Планы полов».

Допущения и предложения на листе

Основа листа: размеры и контуры этажей подобраны проектировщиком по составу помещений и площадям этажей с картинки 470 px (размеры на ней не читаются); обмер и исходный проект — задание (К-1); высоты: 1-й этаж 2800 мм, мансарда 2700 мм (горизонтальная часть) приняты; скаты кровли мансарды приняты по картинке: колено 1200 мм, уклон 45°, конёк вдоль длинной стороны; проект КР — задание (К-2); наружные стены 400 мм, перегородки 120 мм приняты (К-1); разрешённая мощность 15 кВт принята по типовым ТУ для частного дома (К-4); подрайон климата не задан — принят не северный (жилые от 2,5 м) (К-7).

Знак «**» — предложение проектировщика, заказчиком не утверждено (согласовать с заказчиком): записи в реестре нет: плинтус пом. 12 — артикул изделия не выбран: позиция описана характеристиками («аналог по характеристикам»), артикул выбирается при закупке.

См. лист открытых вопросов (лист 7, записи К-1, К-2, К-4, К-7).

1000 мм · печать 1:1

Изм.	Кол.уч	Лист	№ док.	Подп.	Дата
Разраб.		Кырлан А.С.			21.10.26
Пров.					
ГИП					
Н. контр.					
Утв.					

ГД-2026-010-АИ

Дом 331 м²

Общая площадь 270,67* м² · * размеры приняты, не замерены (реестр — л. 7, К-1)

Дизайн-проект интерьера

Стадия	Лист	Листов
РП	63	159

Раскладка плитки. Крыльцо

М 1:20

Кырлан Александр Сергеевич

выпуск 18.10.2026 № 9365d64cec · стр. 67 из 197

Раскладка плитки. Санузел 1 этажа. Развёртки стен

Пом. 3 · вид изнутри помещения · размеры в мм · высоты от чистого пола, отметки от ±0,000

ПРЕДВАРИТЕЛЬНО · не для производства работ · открыто пунктов: 6 (реестр — л. 7)

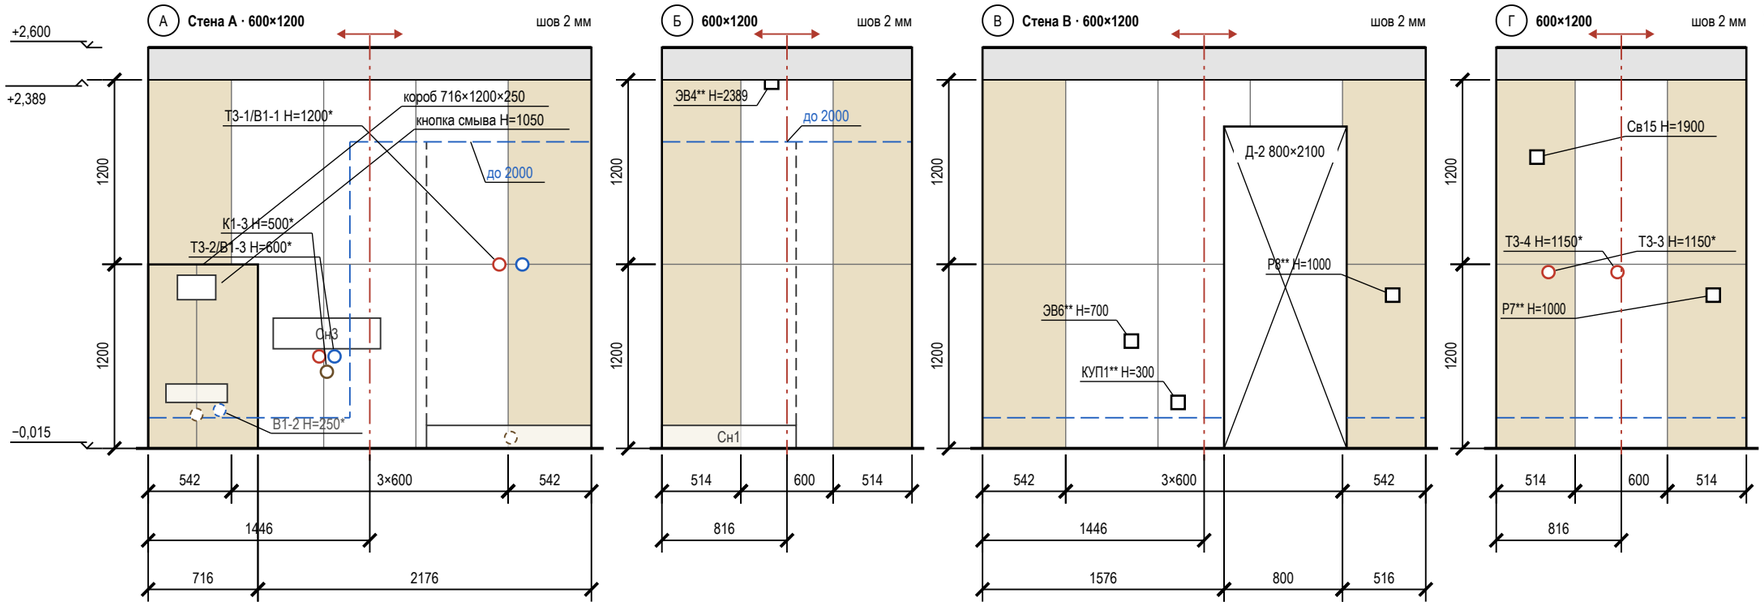

Условные обозначения

- плитка целая; тонкая линия — шов
- плитка с подрезкой (размер — на цепочке)
- ось старта; стрелки — направление укладки
- верх гидроизоляции: 200 от ЧП, в мокрой зоне — «до …»
- проём — не облицовывается
- сантехприбор: габарит, высота по практике
- граница душевой зоны (ограждение)
- короб инсталляции, в нём кнопка смыва 250×160
- вывод В1 (код — в ведомости привязок)
- вывод Т3 (код — в ведомости привязок)
- вывод К1 (код — в ведомости привязок)
- вывод за прибором / в коробе (не на сетке)
- электроточка: марка и Н — по листам ЭОМ
- отметка уровня, м: ±0,000 — чистый пол жилых помещений
- низ потолка; серая полоса — стена без плитки
- А — обозначение стены А–Г (как на развёртках)

Подсчёт плитки по стенам и коробу

Поверхность	L × H, мм	S, м²	Целых	Подр.	С запасом	Подрезки: край / верх, мм
стена А	2892 × 2404	6,21	5	4	10	542 / 542; целый ряд
короб (ст. А)	716×1200×250	1,64	0	6	7	лицо 315 / 399; бок. 250
стена Б	1632 × 2404	4,04	2	4	7	514 / 514; целый ряд
стена В	2892 × 2404	5,39	2	7	10	542 / 542; целый ряд
стена Г	1632 × 2404	4,04	2	4	7	514 / 514; целый ряд
Итого		**21,31**	**11**	**25**	**41**	

Сдвиг точек под раскладку

Точка (ВК, ЭОМ)	Стена	Проект: от угла / Н	Под раскладку: от угла / Н	Сдвиг, мм
Т3-1/В1-1	А	2366 / 1200	2349 / 1141	−17 на шов; Н −59
Т3-2/В1-3, К1-3	А	1166 / 600, 500	1145 / 600, 500	−21 на шов
ЭВ4**	Б	716 / 2389	816 / 2403	+100 в центр плитки; Н +14
Р8**	В	2676 / 1000	2650 / 1000	−26 в центр плитки
КУП1**	В	1276 / 300	1145 / 300	−131 на шов
ЭВ6**	В	971 / 700	844 / 700	−127 в центр плитки
Т3-3	Г	341 / 1150	214 / 1150	−127 в центр плитки
Т3-4	Г	791 / 1150	816 / 1150	+25 в центр плитки
Св15	Г	266 / 1900	214 / 1900	−52 в центр плитки

Примечания

1. Вид изнутри, стены по часовой стрелке А → Г. Высоты — от чистого пола (−0,015), отметки — от ±0,000. Раскладка от чистовых размеров (штукатурка 10 + клей 5 + плитка 9 мм), подрезки чистые; старт — от оси стены, ряды от пола целыми.
2. Верх плитки +2,389, потолок +2,600, зазор 211 мм: потолок ГКЛ опустить до +2,392 (шов 3 мм, герметик) согласовать с монтажником ГКЛ; иначе профиль-окантовка, полосу окрасить в цвет потолка. Подрезной ряд 206 мм не делать.
3. Точки из таблицы сдвигов переносятся до черновой разводки: смеситель — по оси пары В1 + Т3; вывод на оси прибора — вместе с прибором, иначе старт раскладки — на ось прибора.
4. Выводы — по «Плану выводов сантехники», электроточки — по ЭОМ, «*» — высота по практике; за приборами и в коробе (К1-1, В1-2, К1-2) — штриховым кольцом.
5. Гидроизоляция: 200 мм от ЧП по периметру; у душа — до 2000 и 500 мм за поддон (СП 29.13330.2011, п. 7.2 — на высоту замачивания); углы — лентой; акт скрытых работ, пролив.
6. Короб 716×1200×250: лицо 315 / 399 мм от оси кнопки смыва, боковины, полка; углы — запил 45° или профиль; за коробом плитку не кладут.

Допущения и предложения на листе

Основа листа: размеры и контуры этажей подобраны проектировщиком по составу помещений и площадям этажей с картинки 470 px (размеры на ней не читаются); обмер и исходный проект — задание (К-1); высоты: 1-й этаж 2800 мм, мансарда 2700 мм (горизонтальная часть) приняты; скаты кровли мансарды приняты по картинке: колено 1200 мм, уклон 45°, конёк вдоль длинной стороны; проект КР — задание (К-2); наружные стены 400 мм, перегородки 120 мм приняты (К-1); разрешённая мощность 15 кВт принята по типовым ТУ для частного дома (К-4); подрайон климата не задан — принят не северный (жилые от 2,5 м) (К-7).

Знак «**» — предложение проектировщика, заказчиком не утверждено (согласовать с заказчиком): записи в реестре нет: Р7, Р8 — по образцу: Р7, Р8 и Р33 на высоте 1000 мм — верхний предел нормы (ПУЭ, п. 6.6.30, не выше 1 м); флаг решения снят; ЭВ4, КУП1 — по образцу: Добавлены выводы к вентиляторам: ЭВ4 (ВР1, ванная) и ЭВ5 (ВР3, санузел 2) — группа 3, высота 2389 мм, включение с основным светом, таймер выбега в вентиляторе; и коробки уравнивания потенциалов КУП1 (ванная) и КУП2 (санузел 2) — высота 300 мм, у входа, вне зон 0–2, проводник от шины РЕ щита ЩК, сече; ЭВ6 — по образцу: Добавлены электрические полотенцесушители IP44: П10 в ванной (480 мм, низ 900 мм) и П13 в санузле 2 (400 мм, низ 900 мм), выводы ЭВ6 и ЭВ7; мощность группы 13 — 2,4 кВт вместо 1,8 кВт.

См. лист открытых вопросов (лист 7, записи К-1, К-2, К-4, К-7).

1000 мм · печать 1:1

Изм.	Кол.уч	Лист	№ док.	Подп.	Дата	ГД-2026-010-АИ			
						Дом 331 м²			
						Общая площадь 270,67* м² · * размеры приняты, не замерены (реестр — л. 7, К-1)			
Разраб.		Кырлан А.С.			21.10.26	Дизайн-проект интерьера	Стадия	Лист	Листов
Пров.							РП	64	159
ГИП									
Н. контр.						Раскладка плитки. Санузел 1 этажа. Развёртки стен	Кырлан Александр Сергеевич		
Утв.						М 1:40			

выпуск 18.10.2026 № 9365d64cec · стр. 68 из 197

Раскладка плитки. Санузел мастер. Развёртки стен

ПРЕДВАРИТЕЛЬНО · не для производства работ · открыто пунктов: 6 (реестр — л. 7)

Пом. 15 · вид изнутри помещения · размеры в мм · высоты от чистого пола, отметки от ±0,000

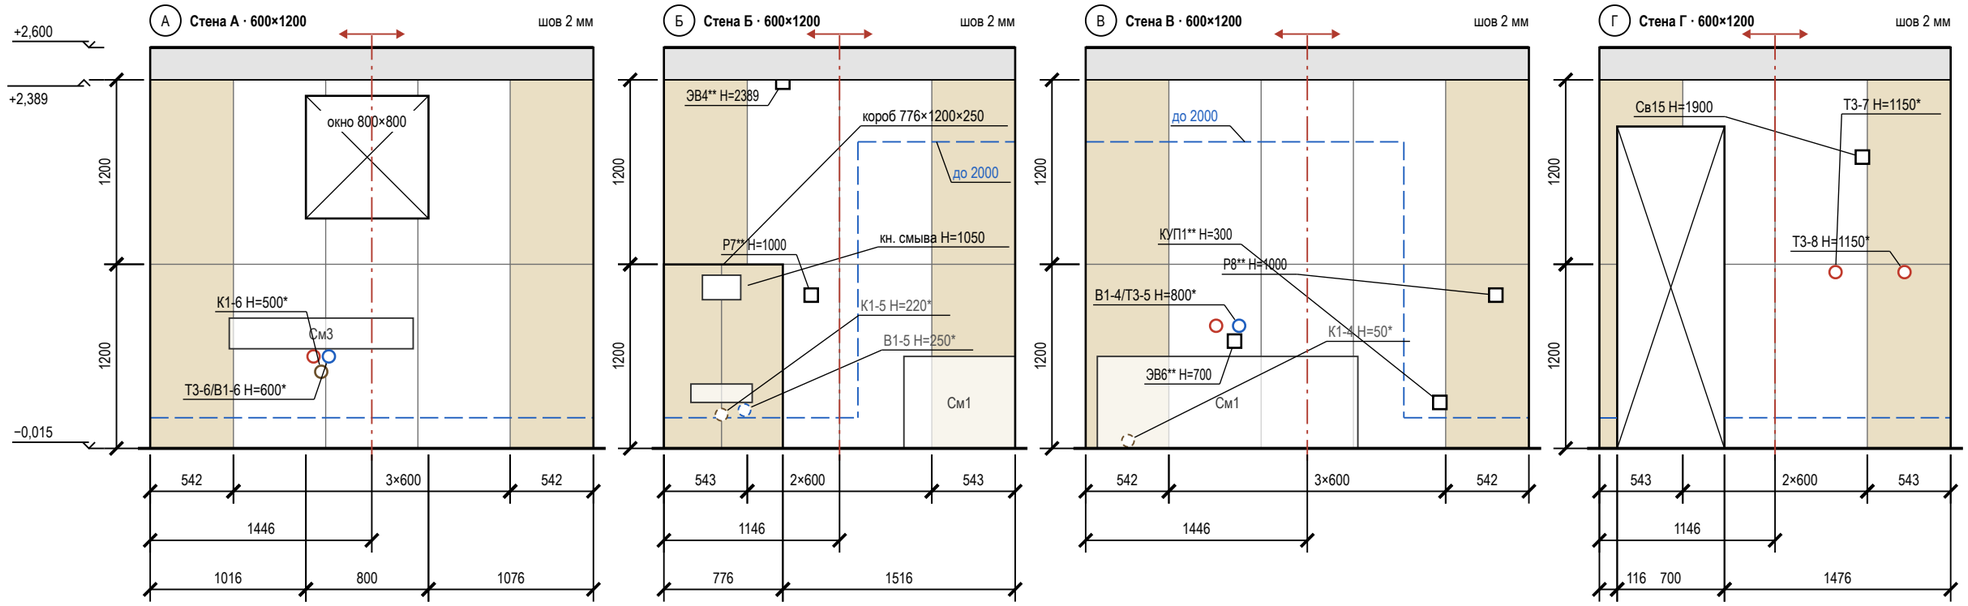

Допущения и предложения на листе. Основа листа: размеры и контуры этажей подобраны проектировщиком по составу помещений и площадям этажей с картинки 470 px (размеры на ней не читаются); обмер и исходный проект — задание (К-1); высоты: 1-й этаж 2800 мм, мансарда 2700 мм (горизонтальная часть) приняты; скаты кровли мансарды приняты по картинке: колено 1200 мм, уклон 45°, конёк вдоль длинной стороны; проект КР — задание (К-2); наружные стены 400 мм, перегородки 120 мм приняты (К-1); разрешённая мощность 15 кВт принята по типовым ТУ для частного дома (К-4); подрайон климата не задан — принят не северный (жилые от 2,5 м) (К-7). Знак «**» — предложение проектировщика, заказчиком не утверждено (согласовать с заказчиком): записи в реестре нет: Р7, Р8 — по образцу: Р7, Р8 и Р33 на высоте 1000 мм — верхний предел нормы (ПУЭ, п. 6.6.30, не выше 1 м); флаг решения снят; ЭВ4, КУП1 — по образцу: Добавлены выводы к вентиляторам: ЭВ4 (ВР1, ванная) и ЭВ5 (ВР3, санузел 2) — группа 3, высота 2389 мм, включение с основным светом, таймер выбега в вентиляторе; и коробки уравнивания потенциалов КУП1 (ванная) и КУП2 (санузел 2) — высота 300 мм, у входа, вне зон 0–2, проводник от шины РЕ щита ЩК, сече; ЭВ6 — по образцу: Добавлены электрические полотенцесушители IP44: П10 в ванной (480 мм, низ 900 мм) и П13 в санузле 2 (400 мм, низ 900 мм), выводы ЭВ6 и ЭВ7; мощность группы 13 — 2,4 кВт вместо 1,8 кВт. См. лист открытых вопросов (лист 7, записи К-1, К-2, К-4, К-7).

Подсчёт плитки по стенам и коробу

Поверхность	L × H, мм	S, м²	Целых	Подр.	С запасом	Подрезки: край / верх, мм
стена А	2892 × 2404	4,54	3	7	11	542 / 542; целый ряд
стена Б	2292 × 2404	3,97	3	4	8	543 / 543; целый ряд
короб (ст. Б)	776×1200×250	1,73	0	6	7	лицо 375 / 399; бок. 250
стена В	2892 × 2404	7,07	6	4	11	542 / 542; целый ряд
стена Г	2292 × 2404	3,43	2	6	9	543 / 543; целый ряд
Итого		**20,73**	**14**	**27**	**46**	

Сдвиг точек под раскладку

Точка (ВК, ЭОМ)	Стена	Проект: от угла / Н	Под раскладку: от угла / Н	Сдвиг, мм
Т3-6/В1-6, К1-6	А	1116 / 600, 500	1145 / 600, 500	+29 на шов
Р7**	Б	961 / 1000	845 / 1000	−116 в центр плитки
ЭВ4**	Б	776 / 2389	845 / 2403	+69 в центр плитки; Н +14
В1-4/Т3-5	В	926 / 800	844 / 800	−82 в центр плитки
Р8**	В	2676 / 1000	2650 / 1000	−26 в центр плитки
КУП1**	В	2311 / 300	2349 / 300	+38 на шов
ЭВ6**	В	971 / 700	844 / 700	−127 в центр плитки
Т3-7	Г	1541 / 1150	1447 / 1150	−94 в центр плитки
Т3-8	Г	1991 / 1150	2049 / 1150	+58 в центр плитки
Св15	Г	1716 / 1900	1748 / 1900	+32 на шов

Условные обозначения

- плитка целая; тонкая линия — шов
- плитка с подрезкой (размер — на цепочке)
- ось старта; стрелки — направление укладки
- верх гидроизоляции: 200 от ЧП, в мокрой зоне — «до …»
- проём — не облицовывается
- сантехприбор: габарит, высота по практике
- короб инсталляции, в нём кнопка смыва 250×160
- вывод В1 (код — в ведомости привязок)
- вывод Т3 (код — в ведомости привязок)
- вывод К1 (код — в ведомости привязок)
- вывод за прибором / в коробе (не на сетке)
- электроточка: марка и Н — по листам ЭОМ
- отметка уровня, м: ±0,000 — чистый пол жилых помещений
- низ потолка; серая полоса — стена без плитки
- обозначение стены А–Г (как на развёртках)

Примечания

1. Вид изнутри, стены по часовой стрелке А → Г. Высоты — от чистого пола (−0,015), отметки — от ±0,000. Раскладка от чистовых размеров (штукатурка 10 + клей 5 + плитка 9 мм), подрезки чистые; старт — от оси стены, ряды от пола целыми.
2. Верх плитки +2,389, потолок +2,600, зазор 211 мм: потолок ГКЛ опустить до +2,392 (шов 3 мм, герметик) — согласовать с монтажником ГКЛ; иначе профиль-окантовка, полосу окрасить в цвет потолка. Подрезной ряд 206 мм не делать.
3. Точки из таблицы сдвигов переносятся до черновой разводки: смеситель — по оси пары В1 + Т3; вывод на оси прибора — вместе с прибором, иначе старт раскладки — на ось прибора.
4. Выводы — по «Плану выводов сантехники», электроточки — по ЭОМ, «*» — высота по практике; за приборами и в коробе (В1-5, К1-5, К1-4) — штриховым кольцом.
5. Гидроизоляция: 200 мм от ЧП по периметру; над ванной — до 2000 и 300 мм за борт (СП 29.13330.2011, п. 7.2 — на высоту замачивания); углы — лентой; акт скрытых работ, пролив.
6. Короб 776×1200×250: лицо 375 / 399 мм от оси кнопки смыва, боковины, полка; углы — запил 45° или профиль; за коробом плитку не кладут.

1000 мм · печать 1:1

Изм.	Кол.уч	Лист	№ док.	Подп.	Дата
Разраб.		Кырлан А.С.			21.10.26
Пров.					
ГИП					
Н. контр.					
Утв.					

ГД-2026-010-АИ

Дом 331 м²

Общая площадь 270,67* м² · * размеры приняты, не замерены (реестр — л. 7, К-1)

Дизайн-проект интерьера

Стадия	Лист	Листов
РП	65	159

Раскладка плитки. Санузел мастер. Развёртки стен

М 1:40

Кырлан Александр Сергеевич

выпуск 18.10.2026 № 9365d64cec · стр. 69 из 197

Раскладка плитки. Санузел 2. Развёртки стен

ПРЕДВАРИТЕЛЬНО · не для производства работ · открыто пунктов: 6 (реестр — л. 7)

Пом. 20 · вид изнутри помещения · размеры в мм · высоты от чистого пола, отметки от ±0,000

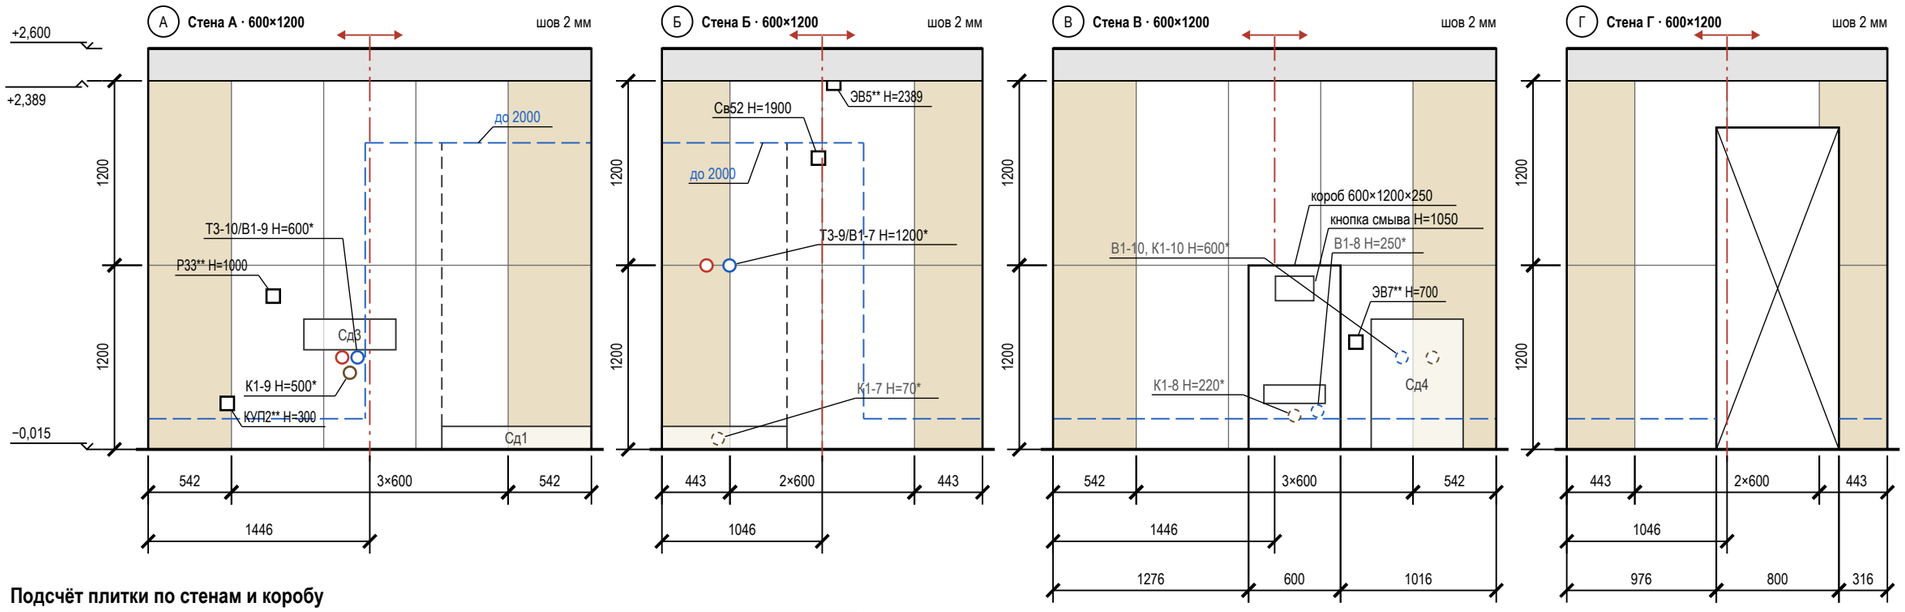

Подсчёт плитки по стенам и коробу

Поверхность	L × H, мм	S, м²	Целых	Подр.	С запасом	Подрезки: край / верх, мм
стена А	2892 × 2404	7,07	6	4	11	542 / 542; целый ряд
стена Б	2092 × 2404	4,42	4	4	9	443 / 443; целый ряд
стена В	2892 × 2404	2,81	4	6	11	542 / 542; целый ряд
короб (ст. В)	600×1200×250	1,47	1	3	5	лицо 600; бок. 250
стена Г	2092 × 2404	2,74	0	7	8	443 / 443; целый ряд
Итого		**18,51**	**15**	**24**	**44**	

Сдвиг точек под раскладку

Точка (ВК, ЭОМ)	Стена	Проект: от угла / Н	Под раскладку: от угла / Н	Сдвиг, мм
Т3-10/В1-9, К1-9	А	1316 / 600, 500	1446 / 600, 500	+130 в центр плитки
Р33**	А	816 / 1000	844 / 1000	+28 в центр плитки
КУП2**	А	516 / 300	543 / 300	+27 на шов
Т3-9/В1-7	Б	366 / 1200	444 / 1141	+78 на шов; Н −59
Св52	Б	1021 / 1900	1046 / 1900	+25 на шов
ЭВ5**	Б	1121 / 2389	1046 / 2343	−75 на шов; Н −46
ЭВ7**	В	1976 / 700	2048 / 700	+72 в центр плитки

Примечания

1. Вид изнутри, стены по часовой стрелке А → Г. Высоты — от чистого пола (−0,015), отметки — от ±0,000. Раскладка от чистовых размеров (штукатурка 10 + клей 5 + плитка 9 мм), подрезки чистые; старт — от оси стены, ряды от пола целыми.
2. Верх плитки +2,389, потолок +2,600, зазор 211 мм: потолок ГКЛ опустить до +2,392 (шов 3 мм, герметик) — согласовать с монтажником ГКЛ; иначе профиль-окантовка, полосу окрасить в цвет потолка. Подрезной ряд 206 мм не делать.
3. Точки из таблицы сдвигов переносятся до черновой разводки: смеситель — по оси пары В1 + Т3; вывод на оси прибора — вместе с прибором, иначе старт раскладки — на ось прибора.
4. Выводы — по «Плану выводов сантехники», электроточки — по ЭОМ, «*» — высота по практике; за приборами и в коробе (К1-7, В1-8, К1-8, В1-10, К1-10) штриховым кольцом.
5. Гидроизоляция: 200 мм от ЧП по периметру; у душа — до 2000 и 500 мм за поддон (СП 29.13330.2011, п. 7.2 — на высоту замачивания); углы — лентой; акт скрытых работ, пролив.
6. Короб 600×1200×250: лицо 600 мм от оси кнопки смыва, боковины, полка; углы — запил 45° или профиль; за коробом плитку не кладут.

Условные обозначения

- плитка целая; тонкая линия — шов
- плитка с подрезкой (размер — на цепочке)
- ось старта; стрелки — направление укладки
- верх гидроизоляции: 200 от ЧП, в мокрой зоне — «до …»
- проём — не облицовывается
- сантехприбор: габарит, высота по практике
- граница душевой зоны (ограждение)
- короб инсталляции, в нём кнопка смыва 250×160
- вывод В1 (код — в ведомости привязок)
- вывод Т3 (код — в ведомости привязок)
- вывод К1 (код — в ведомости привязок)
- вывод за прибором / в коробе (не на сетке)
- электроточка: марка и Н — по листам ЭОМ
- отметка уровня, м: ±0,000 — чистый пол жилых помещений
- низ потолка; серая полоса — стена без плитки
- А — обозначение стены А–Г (как на развёртках)

Допущения и предложения на листе

Основа листа: размеры и контуры этажей подобраны проектировщиком по составу помещений и площадям этажей с картинки 470 px (размеры на ней не читаются); обмер и исходный проект — задание (К-1); высоты: 1-й этаж 2800 мм, мансарда 2700 мм (горизонтальная часть) приняты; скаты кровли мансарды приняты по картинке: колено 1200 мм, уклон 45°, конёк вдоль длинной стороны; проект КР — задание (К-2); наружные стены 400 мм, перегородки 120 мм приняты (К-1); разрешённая мощность 15 кВт принята по типовым ТУ для частного дома (К-4); подрайон климата не задан — принят не северный (жилые от 2,5 м) (К-7).

Знак «**» — предложение проектировщика, заказчиком не утверждено (согласовать с заказчиком): записи в реестре нет: Р33 — по образцу: Розетка Р33 на высоте 1100 мм, вне шва плитки; ЭВ5, КУП2 — по образцу: Добавлены выводы к вентиляторам: ЭВ4 (ВР1, ванная) и ЭВ5 (ВР3, санузел 2) — группа 3, высота 2389 мм, включение с основным светом, таймер выбега в вентиляторе; и коробки уравнивания потенциалов КУП1 (ванная) и КУП2 (санузел 2) — высота 300 мм, у входа, вне зон 0–2, проводник от шины PE щита ЩК, сече; ЭВ7 — по образцу: Добавлены электрические полотенцесушители IP44: П10 в ванной (480 мм, низ 900 мм) и П13 в санузле 2 (400 мм, низ 900 мм), выводы ЭВ6 и ЭВ7; мощность группы 13 — 2,4 кВт вместо 1,8 кВт.

См. лист открытых вопросов (лист 7, записи К-1, К-2, К-4, К-7).

1000 мм · печать 1:1

Изм.	Кол.уч	Лист	№ док.	Подп.	Дата
Разраб.		Кырлан А.С.			21.10.26
Пров.					
ГИП					
Н. контр.					
Утв.					

ГД-2026-010-АИ

Дом 331 м²

Общая площадь 270,67* м² · * размеры приняты, не замерены (реестр — л. 7, К-1)

Дизайн-проект интерьера

Стадия	Лист	Листов
РП	66	159

Раскладка плитки. Санузел 2. Развёртки стен

М 1:40

Кырлан Александр Сергеевич

выпуск 18.10.2026 № 9365d64cec · стр. 70 из 197

План полов · 1-й этаж

Покрытия, направление укладки, отметки чистого пола, стыки · размеры в мм · отметки в м

ПРЕДВАРИТЕЛЬНО · не для производства работ · открыто пунктов: 6 (реестр — л. 7)

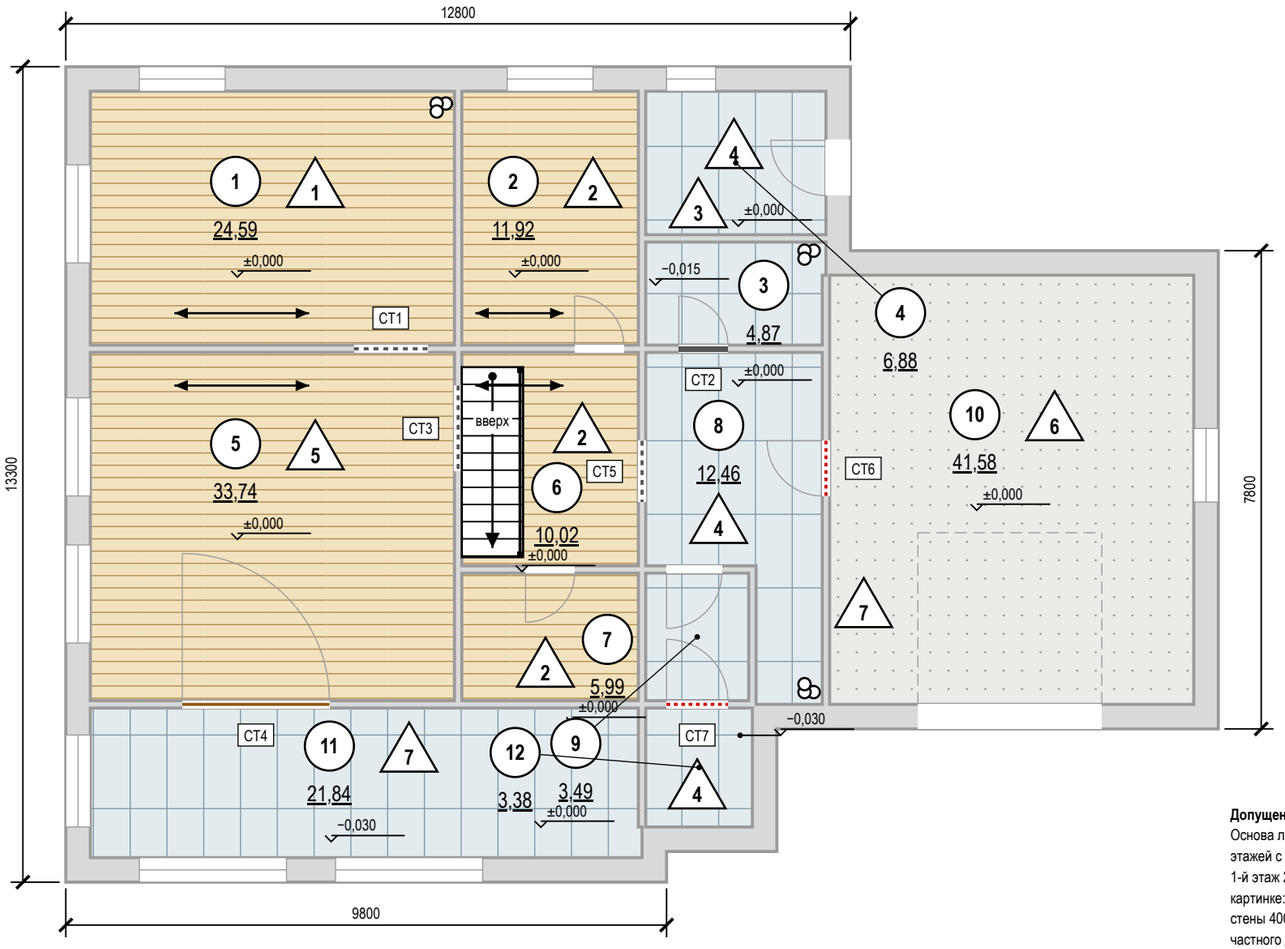

Условные обозначения

- тип 1 — инженерная доска, линии — вдоль доски
- тип 2 — инженерная доска, линии — вдоль доски
- тип 3 — керамогранит 600×1200, сетка — формат плитки
- тип 4 — керамогранит 600×1200, сетка — формат плитки
- тип 5 — инженерная доска, линии — вдоль доски
- тип 6 — наливной пол
- тип 7 — керамогранит 600×1200, сетка — формат плитки
- 1 — номер типа пола (экспликация полов)
- схема пола, без масштаба: плита — штриховка, стяжка — точки, звукоизоляция — зигзаг, гидроизоляция — утолщённая линия с заведением на стену
- направление укладки (длинная сторона доски)
- отметка чистого пола, м
- стык в проёме: без порога (б/п)
- стык в проёме: порог
- стык в проёме: Т-профиль по оси полотна
- стык в проёме: решение не задано
- CT1 — марка стыка (ведомость стыков)
- стояк: К1 — канализация, В1 — ХВС, Т3 — ГВС
- 1 — номер помещения, площадь м²

Отметки по высоте

±0,000	чистый пол пом. 1, 2, 4–10; отсчёт высот
−0,015	чистый пол пом. 3, ниже на 15 мм
−0,030	чистый пол пом. 11, 12, ниже на 30 мм
плита*	верх плиты разный: −0,064, −0,170 (задание на обмер)
сущ. пол	снимается до плиты; не замерен (задание на обмер)

Допущения и предложения на листе

Основа листа: размеры и контуры этажей подобраны проектировщиком по составу помещений и площадям этажей с картинки 470 px (размеры на ней не читаются); обмер и исходный проект — задание (К-1); высоты: 1-й этаж 2800 мм, мансарда 2700 мм (горизонтальная часть) приняты; скаты кровли мансарды приняты по картинке: колено 1200 мм, уклон 45°, конёк вдоль длинной стороны; проект КР — задание (К-2); наружные стены 400 мм, перегородки 120 мм приняты (К-1); разрешённая мощность 15 кВт принята по типовым ТУ для частного дома (К-4); подрайон климата не задан — принят не северный (жилые от 2,5 м) (К-7).

Знак «**» — предложение проектировщика, заказчиком не утверждено (согласовать с заказчиком): записи в реестре нет: плинтус пом. 1, 2, 4–12, фартук пом. 1, акцент пом. 5 — артикул изделия не выбран: позиция описана характеристиками («аналог по характеристикам»), артикул выбирается при закупке; пол пом. 10 — покрытие пола гаража — предложение исполнителя: выдерживает шины, масло и антигололёдные реагенты, без швов.

См. лист открытых вопросов (лист 7, записи К-1, К-2, К-4, К-7).

Примечания

1. За отметку ±0,000 принят чистый пол, не существующий (блок отметок). Площади — по чистым размерам помещений, м²; размеры — в мм.
2. Стык разнотипных покрытий — по оси дверного полотна (под полотном в закрытом положении); решение стыка — по ведомости стыков.
3. Пол санузлов ниже смежных помещений на 15 мм; гидроизоляция по стяжке с заведением на стены не менее 200 мм (СП 29.13330.2011, п. 7.2), до облицовки — тест проливом и акт скрытых работ.
4. Трубопроводы в конструкции пола не прокладываются: пирог пола 49–170 мм не вмещает выпуски канализации с уклоном — выпуски К1 ведутся по стенам над чистым полом в коробах.
5. Штучные покрытия (инженерная доска): направление — по стрелке; влажность основания по СМ не более 2,0 % (по ТУ изготовителя).
6. Ровность основания — просвет под 2-метровой рейкой не более 2 мм: пом. 1, 2, 5, 6, 7 (инженерная доска), пом. 3, 4, 8, 9 (керамогранит), пом. 10 (наливной пол); 3 мм: пом. 11, 12 (керамогранит); проверить до укладки покрытия (СП 71.13330.2017, табл. 8.5).
7. Плавающая стяжка по звукоизоляции: демпферная (кромочная) лента по контуру помещения, у стояков и колонн — до верха чистого пола (СП 51.13330.2011, п. 9.11); плинтус крепится только к стене.
8. Сетка на плитке — условная, в размер формата; точка старта и раскладка — по листу раскладки плитки.
9. Пироги полов — по экспликации полов: слои сверху вниз, толщины в мм; гидроизоляция мокрых зон — в пироге и в ведомости отделки; схема пола — без масштаба.
10. Экспликация полов (ф. 4 прил. А ГОСТ 21.501-2018) и ведомость стыков покрытий — на отдельном листе 69.

1000 мм · печать 1:1

Изм.	Кол.уч	Лист	№ док.	Подп.	Дата
Разраб.		Кырлан А.С.			21.10.26
Пров.					
ГИП					
Н. контр.					
Утв.					

ГД-2026-010-АИ

Дом 331 м²

Общая площадь 270,67* м² · * размеры приняты, не замерены (реестр — л. 7, К-1)

Дизайн-проект интерьера

Стадия	Лист	Листов
РП	67	159

План полов · 1-й этаж

М 1:100

Кырлан Александр Сергеевич

выпуск 18.10.2026 № 9365d64cec · стр. 71 из 197

План полов · Мансарда

Покрытия, направление укладки, отметки чистого пола, стыки · размеры в мм · отметки в м

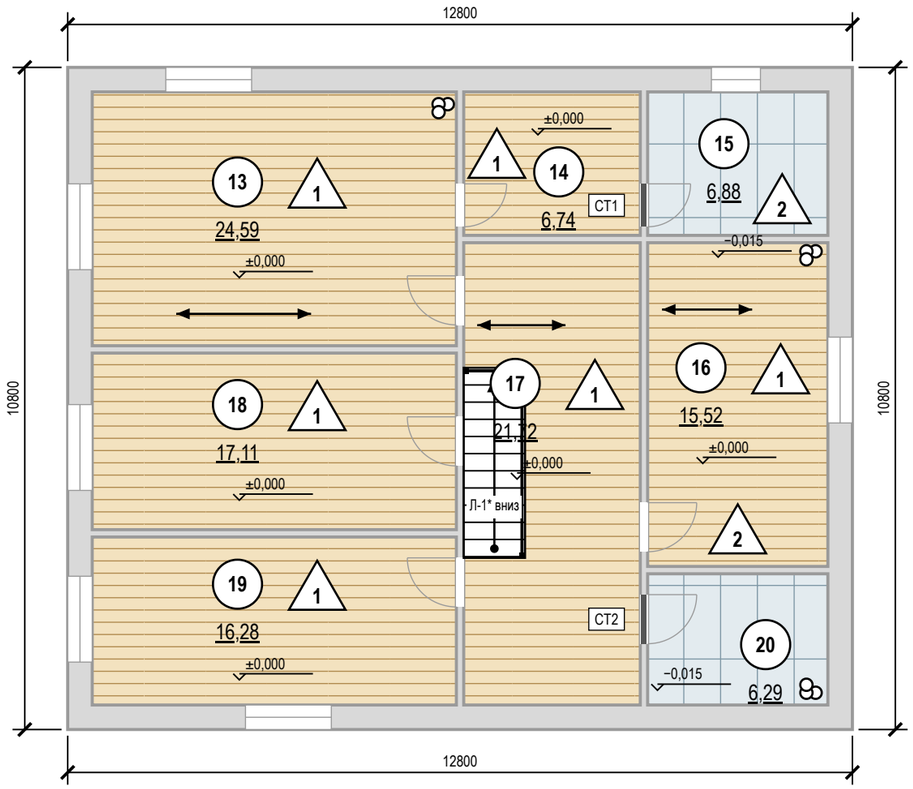

Допущения и предложения на листе

Основа листа: размеры и контуры этажей подобраны проектировщиком по составу помещений и площадям этажей с картинки 470 px (размеры на ней не читаются); обмер и исходный проект — задание (К-1); высоты: 1-й этаж 2800 мм, мансарда 2700 мм (горизонтальная часть) приняты; скаты кровли мансарды приняты по картинке: колено 1200 мм, уклон 45°, конёк вдоль длинной стороны; проект КР — задание (К-2); наружные стены 400 мм, перегородки 120 мм приняты (К-1); разрешённая мощность 15 кВт принята по типовым ТУ для частного дома (К-4); подрайон климата не задан — принят не северный (жилые от 2,5 м) (К-7).

Знак «*» — принято, не замерено и не подтверждено (замерить на объекте): К-6: Л-1 — габарит марша снят с картинки заказчика (11 проступей в холле 3,6 м), а до отм. +3,150 нужно 18 подъёмов — одномаршевая не встаёт: решение по К-6.

Знак «**» — предложение проектировщика, заказчиком не утверждено (согласовать с заказчиком): записи в реестре нет: плинтус пом. 13, 14, 16, 17 — артикул изделия не выбран: позиция описана характеристиками («аналог по характеристикам»), артикул выбирается при закупке.

См. лист открытых вопросов (лист 7, записи К-1, К-2, К-4, К-6, К-7).

Примечания

1. За отметку ±0,000 принят чистый пол, не существующий (блок отметок). Площади — по чистым размерам помещений, м²; размеры — в мм.
2. Стык разнотипных покрытий — по оси дверного полотна (под полотном в закрытом положении); решение стыка — по ведомости стыков.
3. Пол санузлов ниже смежных помещений на 15 мм за счёт меньшей толщины стяжки (верх плиты общий — по экспликации полов); гидроизоляция по стяжке с заведением на стены не менее 200 мм (СП 29.13330.2011, п. 7.2), до облицовки — тест проливом и акт скрытых работ.
4. Трубопроводы в конструкции пола не прокладываются: пирог пола 49–64 мм не вмещает выпуски канализации с уклоном — выпуски К1 ведутся по стенам над чистым полом в коробах.
5. Штучные покрытия (инженерная доска): направление — по стрелке; влажность основания по СМ не более 2,0 % (по ТУ изготовителя).
6. Ровность основания — просвет под 2-метровой рейкой не более 2 мм: пом. 13, 14, 16, 17, 18, 19 (инженерная доска), пом. 15, 20 (керамогранит); проверить до укладки покрытия (СП 71.13330.2017, табл. 8.5).
7. Сетка на плитке — условная, в размер формата; точка старта и раскладка — по листу раскладки плитки.
8. Пироги полов — по экспликации полов: слои сверху вниз, толщины в мм; гидроизоляция мокрых зон — в пироге и в ведомости отделки; схема пола — без масштаба.

1000 мм · печать 1:1

Экспликация полов

Номер помещения	Тип пола	Схема пола	Данные элементов пола (наименование, толщина, основание), мм	Площадь, м²
13, 14, 16, 17, 18, 19	1	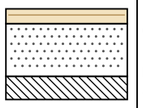	Инженерная доска на клею — 14 Стяжка ЦПС М200 — 50 Плита перекрытия Всего 64 мм; ЧП ±0,000, верх плиты −0,064	101,96
15, 20	2	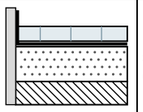	Керамогранит на клею С2 TE S1 — 14 Гидроизоляция обмазочная, 2 слоя, с заведением на стены 200 мм — 2 Стяжка ЦПС М200 — 33 Плита перекрытия Всего 49 мм; ЧП −0,015, верх плиты −0,064	13,17
			Итого	**115,13**

Стыки покрытий в проёмах

Марка	Проём	Типы пола	Отметки ЧП	Решение
СТ1	15–14 (Д-9)	2 / 1	−0,015 / ±0,000	порог h=15 мм
СТ2	20–17 (Д-13)	2 / 1	−0,015 / ±0,000	порог h=15 мм

Условные обозначения

- тип 1 — инженерная доска, линии — вдоль доски
- тип 2 — керамогранит 600×1200, сетка — формат плитки
- 1 — номер типа пола (экспликация полов)
- схема пола, без масштаба: плита — штриховка, стяжка — точки, звукоизоляция — зигзаг, гидроизоляция — утолщённая линия с заведением на стену
- направление укладки (длинная сторона доски)
- ±0,000 — отметка чистого пола, м
- стык в проёме: порог
- СТ1 — марка стыка (ведомость стыков)
- стояк: К1 — канализация, В1 — ХВС, Т3 — ГВС
- (1) — номер помещения, площадь м²

Отметки по высоте

±0,000	чистый пол пом. 13, 14, 16–19; отсчёт высот
−0,015	чистый пол пом. 15, 20, ниже на 15 мм
−0,064*	верх плиты — расчёт, не замер (задание на обмер)
сущ. пол	снимается до плиты; не замерен (задание на обмер)

Изм.	Кол.уч	Лист	№ док.	Подп.	Дата
Разраб.		Кырлан А.С.			21.10.26
Пров.					
ГИП					
Н. контр.					
Утв.					

ГД-2026-010-АИ

Дом 331 м²

Общая площадь 270,67* м² · * размеры приняты, не замерены (реестр — л. 7, К-1)

Дизайн-проект интерьера

Стадия	Лист	Листов
РП	68	159

План полов · Мансарда

М 1:100

Кырлан Александр Сергеевич

выпуск 18.10.2026 № 9365d64cec · стр. 72 из 197

Конструкции полов и стыки покрытий

Форма 4 прил. А ГОСТ 21.501-2018 · толщины в мм · отметки в м

ПРЕДВАРИТЕЛЬНО · не для производства работ · открыто пунктов: 6 (реестр — л. 7)

Экспликация полов

Номер помещения	Тип пола	Схема пола	Данные элементов пола (наименование, толщина, основание), мм	Площадь, м²
1	1	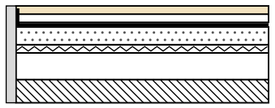	Инженерная доска дуб на клею — 14 Клей паркетный МС-полимерный — 1 Гидроизоляция полиуретановая, 2 слоя (зона мойки и острова) — 2 Стяжка ЦПС М300 (В22,5), фибра, по звукоизоляции — 53 Звукоизоляция — минплита 110 кг/м³ — 20 Засыпка керамзитовая фр. 0–5, уплотнённая — 80 Плита перекрытия монолитная Всего 170 мм; ЧП ±0,000, верх плиты −0,170	24,59
2, 6, 7, 13, 14, 16, 17, 18, 19	2	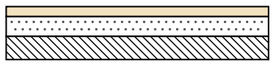	Инженерная доска на клею — 14 Стяжка ЦПС М200 — 50 Плита перекрытия Всего 64 мм; ЧП ±0,000, верх плиты −0,064	129,89
3, 15, 20	3	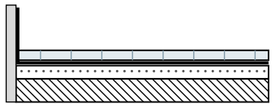	Керамогранит на клею С2 TE S1 — 14 Гидроизоляция обмазочная, 2 слоя, с заведением на стены 200 мм — 2 Стяжка ЦПС М200 — 33 Плита перекрытия Всего 49 мм; ЧП −0,015, верх плиты −0,064	18,04
4, 8, 9	4	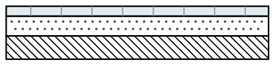	Керамогранит на клею С2 TE S1 — 14 Стяжка ЦПС М200 — 50 Плита перекрытия Всего 64 мм; ЧП ±0,000, верх плиты −0,064	22,83
5	5	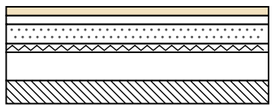	Инженерная доска дуб на клею — 14 Клей паркетный МС-полимерный — 1 Стяжка ЦПС М300 (В22,5), фибра, по звукоизоляции — 55 Звукоизоляция — минплита 110 кг/м³ — 20 Засыпка керамзитовая фр. 0–5, уплотнённая — 80 Плита перекрытия монолитная Всего 170 мм; ЧП ±0,000, верх плиты −0,170	33,74
10	6	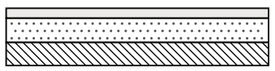	Наливной полимерный пол с грунтом и кварцевой посыпкой — 3 Стяжка ЦПС М300, армированная сеткой — 61 Плита перекрытия по грунту Всего 64 мм; ЧП ±0,000, верх плиты −0,064	41,58
11, 12	7	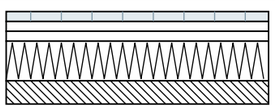	Керамогранит 600×600×10 — 10 Клей плиточный С2 TE S1 (деформируемый) — 5 Сборное основание ГВЛВ 2×12,5 — 25 Пенополистирол экструзионный 2×50 — 100 Плита перекрытия монолитная Всего 140 мм; ЧП −0,030, верх плиты −0,170	25,22
			Итого	**295,89**

Стыки покрытий в проёмах

Марка	Проём	Типы пола	Отметки ЧП	Решение
СТ1	1–5 (Пр-1)	1 / 5	±0,000 / ±0,000	б/п
СТ2	3–8 (Д-2)	3 / 4	−0,015 / ±0,000	порог h=15 мм
СТ3	5–6 (Пр-2)	5 / 2	±0,000 / ±0,000	б/п
СТ4	5–11 (Д-4)	5 / 7	±0,000 / −0,030	Т-профиль
СТ5	8–6 (Пр-3)	4 / 2	±0,000 / ±0,000	б/п
СТ6	8–10 (Д-5)	4 / 6	±0,000 / ±0,000	не задано
СТ7	9–12 (Д-вх)	4 / 7	±0,000 / −0,030	не задано
СТ8	15–14 (Д-9)	3 / 2	−0,015 / ±0,000	порог h=15 мм
СТ9	20–17 (Д-13)	3 / 2	−0,015 / ±0,000	порог h=15 мм

Условные обозначения

схема пола, без масштаба: плита — штриховка, стяжка — точки, звукоизоляция — зигзаг, гидроизоляция — утолщённая линия с заведением на стену

стык в проёме: без порога (б/п)

стык в проёме: порог

стык в проёме: Т-профиль по оси полотна

стык в проёме: решение не задано

СТ1 — марка стыка (ведомость стыков)

Примечания

1. Экспликация полов — по форме 4 прил. А ГОСТ 21.501-2018: слои пирога сверху вниз, толщины в мм; схема пола — без масштаба.
2. Номера помещений, площади, отметки чистого пола, направление укладки и места стыков — по листу «План полов»; привязка марок стыков (СТ) на плане полов, тип каждой схемы пола — в строке экспликации.
3. Стык разнотипных покрытий — по оси дверного полотна (под полотном в закрытом положении).
4. Плавающая стяжка по звукоизоляции: демпферная (кромочная) лента по контуру помещения, у стояков и колонн — до верха чистого пола (СП 51.13330.2011, п. 9.11); плинтус крепится только к стене.
5. Гидроизоляция мокрых зон — с заведением на стены не менее 200 мм (СП 29.13330.2011, п. 7.2); до облицовки — тест проливом и акт скрытых работ.

Допущения и предложения на листе

Основа листа: размеры и контуры этажей подобраны проектировщиком по составу помещений и площадям этажей с картинки 470 px (размеры на ней не читаются); обмер и исходный проект — задание (К-1); высоты: 1-й этаж 2800 мм, мансарда 2700 мм (горизонтальная часть) приняты; скаты кровли мансарды приняты по картинке: колено 1200 мм, уклон 45°, конёк вдоль длинной стороны; проект КР — задание (К-2); наружные стены 400 мм, перегородки 120 мм приняты (К-1); разрешённая мощность 15 кВт принята по типовым ТУ для частного дома (К-4); подрайон климата не задан — принят не северный (жилые от 2,5 м) (К-7).

См. лист открытых вопросов (лист 7, записи К-1, К-2, К-4, К-7).

Изм.	Кол.уч	Лист	№ док.	Подп.	Дата
Разраб.		Кырлан А.С.			21.10.26
Пров.					
ГИП					
Н. контр.					
Утв.					

ГД-2026-010-АИ

Дом 331 м²

Общая площадь 270,67* м² · * размеры приняты, не замерены (реестр — л. 7, К-1)

Дизайн-проект интерьера

Стадия	Лист	Листов
РП	69	159

Конструкции полов и стыки покрытий

М б/м

Кырлан Александр Сергеевич

выпуск 18.10.2026 № 9365d64cec · стр. 73 из 197

Ведомость отделки помещений. Лист 1 из 3

Потолки, стены, низ стен, полы · площади в м², длины в м · отметки в м

Ведомость отделки помещений (форма 1 прил. А ГОСТ 21.501-2018). Лист 1 из 3

№	Наименование помещения	Потолок			Стены и перегородки			Низ стен (плинтус)			Пол		Примечание
		Вид отделки	Код цвета	S, м²	Вид отделки	Код цвета	S, м²	Вид отделки	Код цвета	L, м	Вид отделки	S, м²	
1	Кухня-столовая 24,59 м²	ГКЛ по каркасу П113, отм. +2,700; +2,550; +2,600; окраска, Tikkurila Luja 7, матовая, 2 слоя, подготовка Q3	NCS S 0804-Y30R	24,59	Окраска, Tikkurila Luja 7, полуматовая, 2 слоя, подготовка К3 Фартук кухни (стена А): облицовка керамогранитом, аналог: керамогранит матовый, тон F497, 600×600×9 мм, клей C2 TE S1, затирка CG2WA	NCS S 0804-Y30R #F1F1EC	45,02 0,93	Плинтус МДФ h=80 мм, аналог: МДФ под окраску 80×16 мм	NCS S 0804-Y30R	18,3	Инженерная доска, 1167-4250, 2100×127 мм, на клею; тип 1, отм. ЧП ±0,000	24,59	Н стен 2700 (до потолка); влагостойкая полуматовая окраска (класс мокрого истирания 1 по EN 13300); категория К3 по СП 71.13330.2017, табл. 7.5; по ГКЛ каркаса П113, влагостойкая окраска; Q3 колеруется в код стен, но по эмали на МДФ: сличать отдельным выкрасом на своей подложке (выкрас № 10); плинтус в цвет: стены
2	Кабинет-гостевая 11,92 м²	ГКЛ по каркасу П113, отм. +2,700; +2,600; окраска, Tikkurila Anti-Reflex 2, глубокоматовая, 2 слоя, подготовка Q3	Little Greene No. 105	11,92	Окраска, Farrow & Ball Modern Emulsion, матовая, 2 слоя, подготовка Q3 Акцент — стена А: окраска, Farrow & Ball Modern Emulsion, матовая, 2 слоя, подготовка Q3	Farrow & Ball No. 226 Farrow & Ball No. 298	25,30 5,68	Плинтус МДФ h=80 мм, аналог: МДФ под покраску 80×16	Farrow & Ball No. 226	11,7	Инженерная доска, 1167-4250, 2100×127 мм, на клею; тип 2, отм. ЧП ±0,000	11,92	Н стен 2700 (до потолка); плинтус в цвет: стены
3	Санузел 1 этажа 4,87 м²	ГКЛВ по каркасу П113, отм. +2,600; окраска, Tikkurila Luja 7, матовая, 2 слоя, подготовка Q3	Little Greene No. 105	4,87	Облицовка плиткой, A8UZ, 600×1200×9 мм, клей C2 TE S1, затирка CG2WA	Atlas Concorde A8UZ	20,53	нет			Керамогранит, A8UZ, 600×1200×9 мм; тип 3, отм. ЧП −0,015	4,87	Н стен 2615 (до потолка); гидроизоляция обмазочная, 2 слоя, с заведением на стены 200 мм (по пирогу пола); тест проливом и акт скрытых работ
4	Котельная 6,88 м²	Окраска, Tikkurila Anti-Reflex 2, глубокоматовая, 2 слоя, подготовка Q3	Little Greene No. 105	6,88	Окраска, Farrow & Ball Modern Emulsion, матовая, 2 слоя, подготовка Q3	Farrow & Ball No. 226	26,96	Плинтус МДФ h=80 мм, аналог: МДФ под покраску 80×16	Farrow & Ball No. 226	9,7	Керамогранит, A8UZ, 600×1200×9 мм; тип 4, отм. ЧП ±0,000	6,88	Н стен 2800 (до потолка); матовая моющаяся, класс 1 EN 13300 — осознанно вместо полуматовой; плинтус в цвет: стены
5	Гостиная 33,74 м²	ГКЛ по каркасу П113, отм. +2,600; +2,700; окраска, Tikkurila Anti-Reflex 2, глубокоматовая, 2 слоя, подготовка Q3	NCS S 0804-Y30R	33,74	Окраска, Tikkurila Optiva 5 Matt, матовая, 2 слоя, подготовка К3 Акцент — стена А: окраска, Tikkurila Optiva 5 Matt, матовая, 3 слоя, подготовка К3	NCS S 0804-Y30R Farrow & Ball No. 93	32,20 12,92	Плинтус МДФ h=80 мм, аналог: МДФ под окраску 80×16 мм	NCS S 0804-Y30R	18,2	Инженерная доска, 1167-4250, 2100×127 мм, на клею; тип 5, отм. ЧП ±0,000	33,74	Н стен 2600 (до потолка); колеруется в код стен, но по эмали на МДФ: сличать отдельным выкрасом на своей подложке (выкрас № 10); плинтус в цвет: стены
6	Холл с лестницей 10,02 м²	ГКЛ по каркасу П113, отм. +2,700; окраска, Tikkurila Anti-Reflex 2, глубокоматовая, 2 слоя, подготовка Q3	Little Greene No. 105	10,02	Окраска, Farrow & Ball Modern Emulsion, матовая, 2 слоя, подготовка Q3	Farrow & Ball No. 226	22,29	Плинтус МДФ h=80 мм, аналог: МДФ под покраску 80×16	Farrow & Ball No. 226	7,0	Инженерная доска, 1167-4250, 2100×127 мм, на клею; тип 2, отм. ЧП ±0,000	10,02	Н стен 2700 (до потолка); матовая моющаяся, класс 1 EN 13300 — осознанно вместо полуматовой; плинтус в цвет: стены
7	Кладовая 5,99 м²	Окраска, Tikkurila Anti-Reflex 2, глубокоматовая, 2 слоя, подготовка Q3	Little Greene No. 105	5,99	Окраска, Tikkurila Harmony, матовая, 2 слоя, подготовка Q3	Little Greene No. 105	23,28	Плинтус МДФ h=80 мм, аналог: МДФ под покраску 80×16	Little Greene No. 105	7,8	Инженерная доска, 1167-4250, 2100×127 мм, на клею; тип 2, отм. ЧП ±0,000	5,99	Н стен 2800 (до потолка); плинтус в цвет: стены
8	Прихожая 12,46 м²	ГКЛ по каркасу П113, отм. +2,700; окраска, Tikkurila Anti-Reflex 2, глубокоматовая, 2 слоя, подготовка Q3	Little Greene No. 105	12,46	Окраска, Farrow & Ball Modern Emulsion, матовая, 2 слоя, подготовка Q3	Farrow & Ball No. 226	38,99	Плинтус МДФ h=80 мм, аналог: МДФ под покраску 80×16	Farrow & Ball No. 226	13,6	Керамогранит, A8UZ, 600×1200×9 мм; тип 4, отм. ЧП ±0,000	12,46	Н стен 2700 (до потолка); матовая моющаяся, класс 1 EN 13300 — осознанно вместо полуматовой; плинтус в цвет: стены

Примечания

1. Ведомость продолжена на листе 2 из 3; итоги, сводка площадей и примечания — на последнем листе ведомости.

Допущения и предложения на листе

Основа листа: размеры и контуры этажей подобраны проектировщиком по составу помещений и площадям этажей с картинки 470 px (размеры на ней не читаются); обмер и исходный проект — задание (К-1); высоты: 1-й этаж 2800 мм, мансарда 2700 мм (горизонтальная часть) приняты; скаты кровли мансарды приняты по картинке: колено 1200 мм, уклон 45°, конёк вдоль длинной стороны; проект КР — задание (К-2); наружные стены 400 мм, перегородки 120 мм приняты (К-1); разрешённая мощность 15 кВт принята по типовым ТУ для частного дома (К-4); подрайон климата не задан — принят не северный (жилые от 2,5 м) (К-7).

Знак «**» — предложение проектировщика, заказчиком не утверждено (согласовать с заказчиком): записи в реестре нет: плинтус пом. 1, 2, 4–14, 16, 17, фартук пом. 1, акцент пом. 5 — артикул изделия не выбран: позиция описана характеристиками («аналог по характеристикам»), артикул выбирается при закупке; пол пом. 10 — покрытие пола гаража — предложение исполнителя: выдерживает шины, масло и антигололёдные реагенты, без швов.

См. лист открытых вопросов (лист 7, записи К-1, К-2, К-4, К-7).

Изм.	Кол.уч	Лист	№ док.	Подп.	Дата
Разраб.		Кырлан А.С.			21.10.26
Пров.					
ГИП					
Н. контр.					
Утв.					

ГД-2026-010-АИ

Дом 331 м²

Общая площадь 270,67* м² · * размеры приняты, не замерены (реестр — л. 7, К-1)

Дизайн-проект интерьера	Стадия	Лист	Листов
	РП	70	159

Ведомость отделки помещений. Лист 1 из 3

М б/м

Кырлан Александр Сергеевич

выпуск 18.10.2026 № 9365d64cec · стр. 74 из 197

Ведомость отделки помещений. Лист 2 из 3

Потолки, стены, низ стен, полы · площади в м², длины в м · отметки в м

Ведомость отделки помещений (форма 1 прил. А ГОСТ 21.501-2018). Лист 2 из 3

№	Наименование помещения	Потолок			Стены и перегородки			Низ стен (плинтус)			Пол		Примечание
		Вид отделки	Код цвета	S, м²	Вид отделки	Код цвета	S, м²	Вид отделки	Код цвета	L, м	Вид отделки	S, м²	
9	Тамбур 3,49 м²	Окраска, Tikkurila Anti-Reflex 2, глубокоматовая, 2 слоя, подготовка Q3	Little Greene No. 105	3,49	Окраска, Farrow & Ball Modern Emulsion, матовая, 2 слоя, подготовка Q3	Farrow & Ball No. 226	17,07	Плинтус МДФ h=80 мм, аналог: МДФ под покраску 80×16	Farrow & Ball No. 226	5,6	Керамогранит, A8UZ, 600×1200×9 мм; тип 4, отм. ЧП ±0,000	3,49	Н стен 2800 (до потолка); матовая моющаяся, класс 1 EN 13300 — осознанно вместо полуматовой; плинтус в цвет: стены
10	Гараж 41,58 м²	Окраска, Tikkurila Anti-Reflex 2, глубокоматовая, 2 слоя, подготовка Q3	Little Greene No. 105	41,58	Окраска, Farrow & Ball Modern Emulsion, матовая, 2 слоя, подготовка Q3	Farrow & Ball No. 226	62,59	Плинтус ПВХ h=100 мм, аналог: ПВХ влагостойкий 100 мм, серый		22,0	Аналог: наливной полимерный пол (эпоксидный), с кварцевой посыпкой, 3 мм; тип 6, отм. ЧП ±0,000	41,58	Н стен 2800 (до потолка); матовая моющаяся, класс 1 EN 13300 — осознанно вместо полуматовой
11	Веранда 21,84 м²	Окраска, Tikkurila Luja 7, матовая, 2 слоя, подготовка Q3	NCS S 0804-Y30R	21,84	Окраска, Tikkurila Luja 7, полуматовая, 2 слоя, подготовка К3	NCS S 0804-Y30R	49,63	Плинтус из керамогранита h=80 мм, аналог: из керамогранита пола, подрезка 80 мм, верхняя кромка с запилом 45°	#B8AFA5	20,5	Керамогранит, A8UZ, 600×1200×10 мм; тип 7, отм. ЧП −0,030	21,84	Н стен 2830 (до потолка); влагостойкая окраска по утеплённой стене; категория К3 по СП 71.13330.2017, табл. 7.5; по ГКЛВ каркаса П113, влагостойкая окраска; Q3
12	Крыльцо 3,38 м²	Окраска, Tikkurila Luja 7, матовая, 2 слоя, подготовка Q3	NCS S 0804-Y30R	3,38	Окраска, Tikkurila Luja 7, полуматовая, 2 слоя, подготовка К3	NCS S 0804-Y30R	18,73	Плинтус из керамогранита h=80 мм, аналог: из керамогранита пола, подрезка 80 мм, верхняя кромка с запилом 45°	#B8AFA5	6,4	Керамогранит, A8UZ, 600×1200×10 мм; тип 7, отм. ЧП −0,030	3,38	Н стен 2830 (до потолка); влагостойкая окраска по утеплённой стене; категория К3 по СП 71.13330.2017, табл. 7.5; по ГКЛВ каркаса П113, влагостойкая окраска; Q3
13	Спальня мастер 24,59 м²	ГКЛ по каркасу П113, отм. +2,500; +2,600; окраска, Tikkurila Anti-Reflex 2, глубокоматовая, 2 слоя, подготовка Q3	Little Greene No. 105	27,05	Окраска, Farrow & Ball Modern Emulsion, матовая, 2 слоя, подготовка Q3 Акцент — стена А: окраска, Farrow & Ball Modern Emulsion, матовая, 2 слоя, подготовка Q3	Farrow & Ball No. 226 NCS S 7020-G10Y	28,61 7,60	Плинтус МДФ h=80 мм, аналог: МДФ под покраску 80×16	Farrow & Ball No. 226	18,7	Инженерная доска, 1167-4250, 2100×127 мм, на клею; тип 2, отм. ЧП ±0,000	24,59	Н стен 2500 (до потолка); плинтус в цвет: стены
14	Гардеробная мастер 6,74 м²	Окраска, Tikkurila Anti-Reflex 2, глубокоматовая, 2 слоя, подготовка Q3	Little Greene No. 105	8,56	Окраска, Tikkurila Harmony, матовая, 2 слоя, подготовка Q3	Little Greene No. 105	18,68	Плинтус МДФ h=80 мм, аналог: МДФ под покраску 80×16	Little Greene No. 105	9,0	Инженерная доска, 1167-4250, 2100×127 мм, на клею; тип 2, отм. ЧП ±0,000	6,74	Н стен 2700 (до потолка); плинтус в цвет: стены
15	Санузел мастер 6,88 м²	ГКЛВ по каркасу П113, отм. +2,600; окраска, Tikkurila Luja 7, матовая, 2 слоя, подготовка Q3	Little Greene No. 105	7,84	Облицовка плиткой, A8UZ, 600×1200×9 мм, клей C2 TE S1, затирка CG2WA	Atlas Concorde A8UZ	19,94	нет			Керамогранит, A8UZ, 600×1200×9 мм; тип 3, отм. ЧП −0,015	6,88	Н стен 2615 (до потолка); гидроизоляция обмазочная, 2 слоя, с заведением на стены 200 мм (по пирогу пола); тест проливом и акт скрытых работ
16	Спальня 2 15,52 м²	ГКЛ по каркасу П113, отм. +2,600; +2,500; окраска, Tikkurila Anti-Reflex 2, глубокоматовая, 2 слоя, подготовка Q3	Little Greene No. 105	15,52	Окраска, Farrow & Ball Modern Emulsion, матовая, 2 слоя, подготовка Q3 Акцент — стена А: окраска, Farrow & Ball Modern Emulsion, матовая, 2 слоя, подготовка Q3	Farrow & Ball No. 226 Farrow & Ball No. 64	28,08 7,35	Плинтус МДФ h=80 мм, аналог: МДФ под покраску 80×16	Farrow & Ball No. 226	14,7	Инженерная доска, 1167-4250, 2100×127 мм, на клею; тип 2, отм. ЧП ±0,000	15,52	Н стен 2500 (до потолка); плинтус в цвет: стены
17	Холл мансарды 21,72 м²	ГКЛ по каркасу П113, отм. +2,600; окраска, Tikkurila Anti-Reflex 2, глубокоматовая, 2 слоя, подготовка Q3	Little Greene No. 105	23,52	Окраска, Farrow & Ball Modern Emulsion, матовая, 2 слоя, подготовка Q3	Farrow & Ball No. 226	34,75	Плинтус МДФ h=80 мм, аналог: МДФ под покраску 80×16	Farrow & Ball No. 226	14,4	Инженерная доска, 1167-4250, 2100×127 мм, на клею; тип 2, отм. ЧП ±0,000	21,72	Н стен 2600 (до потолка); матовая моющаяся, класс 1 EN 13300 — осознанно вместо полуматовой; плинтус в цвет: стены

Примечания

1. Ведомость продолжена на листе 3 из 3; итоги, сводка площадей и примечания — на последнем листе ведомости.

Допущения и предложения на листе

Основа листа: размеры и контуры этажей подобраны проектировщиком по составу помещений и площадям этажей с картинки 470 px (размеры на ней не читаются); обмер и исходный проект — задание (К-1); высоты: 1-й этаж 2800 мм, мансарда 2700 мм (горизонтальная часть) приняты; скаты кровли мансарды приняты по картинке: колено 1200 мм, уклон 45°, конёк вдоль длинной стороны; проект КР — задание (К-2); наружные стены 400 мм, перегородки 120 мм приняты (К-1); разрешённая мощность 15 кВт принята по типовым ТУ для частного дома (К-4); подрайон климата не задан — принят не северный (жилые от 2,5 м) (К-7).

Знак «**» — предложение проектировщика, заказчиком не утверждено (согласовать с заказчиком): записи в реестре нет: плинтус пом. 1, 2, 4–14, 16, 17, фартук пом. 1, акцент пом. 5 — артикул изделия не выбран: позиция описана характеристиками («аналог по характеристикам»), артикул выбирается при закупке; пол пом. 10 — покрытие пола гаража — предложение исполнителя: выдерживает шины, масло и антигололёдные реагенты, без швов.

См. лист открытых вопросов (лист 7, записи К-1, К-2, К-4, К-7).

Изм.	Кол.уч	Лист	№ док.	Подп.	Дата
Разраб.		Кырлан А.С.			21.10.26
Пров.					
ГИП					
Н. контр.					
Утв.					

ГД-2026-010-АИ

Дом 331 м²

Общая площадь 270,67* м² · * размеры приняты, не замерены (реестр — л. 7, К-1)

Дизайн-проект интерьера	Стадия	Лист	Листов
	РП	71	159

Ведомость отделки помещений. Лист 2 из 3

М б/м

Кырлан Александр Сергеевич

выпуск 18.10.2026 № 9365d64cec · стр. 75 из 197

Ведомость отделки помещений. Лист 3 из 3

Потолки, стены, низ стен, полы · площади в м², длины в м · отметки в м

Ведомость отделки помещений (форма 1 прил. А ГОСТ 21.501-2018). Лист 3 из 3

№	Наименование помещения	Потолок			Стены и перегородки			Низ стен (плинтус)			Пол		Примечание
		Вид отделки	Код цвета	S, м²	Вид отделки	Код цвета	S, м²	Вид отделки	Код цвета	L, м	Вид отделки	S, м²	
18	Спальня 3 17,11 м²	ГКЛ по каркасу П113, отм. +2,500; +2,600; окраска, Tikkurila Anti-Reflex 2, глубокоматовая, 2 слоя, подготовка Q3	Little Greene No. 105	17,11	Окраска, Farrow & Ball Modern Emulsion, матовая, 2 слоя, подготовка Q3 Акцент — стена А: окраска, Farrow & Ball Modern Emulsion, матовая, 2 слоя, подготовка Q3	Farrow & Ball No. 226 NCS S 3020-G30Y	25,47 12,33	Плинтус МДФ h=69 мм, SX165	Farrow & Ball No. 226	15,6	Инженерная доска, 1167-4250, 2100×127 мм, на клею; тип 2, отм. ЧП ±0,000	17,11	Н стен 2500 (до потолка); плинтус в цвет: стены
19	Спальня 4 16,28 м²	ГКЛ по каркасу П113, отм. +2,500; +2,600; окраска, Tikkurila Anti-Reflex 2, глубокоматовая, 2 слоя, подготовка Q3	Little Greene No. 105	18,76	Окраска, Farrow & Ball Modern Emulsion, матовая, 2 слоя, подготовка Q3 Акцент — стена А: окраска, Farrow & Ball Modern Emulsion, матовая, 2 слоя, подготовка Q3	Farrow & Ball No. 226 NCS S 3040-Y70R	15,83 14,85	Плинтус МДФ h=69 мм, SX165	Farrow & Ball No. 226	16,6	Инженерная доска, 1167-4250, 2100×127 мм, на клею; тип 2, отм. ЧП ±0,000	16,28	Н стен 2500 (до потолка); плинтус в цвет: стены
20	Санузел 2 6,29 м²	ГКЛВ по каркасу П113, отм. +2,600; окраска, Tikkurila Luja 7, матовая, 2 слоя, подготовка Q3	Little Greene No. 105	8,15	Облицовка плиткой, A8UZ, 600×1200×9 мм, клей C2 TE S1, затирка CG2WA	Atlas Concorde A8UZ	17,76	нет			Керамогранит, A8UZ, 600×1200×9 мм; тип 3, отм. ЧП −0,015	6,29	Н стен 2615 (до потолка); гидроизоляция обмазочная, 2 слоя, с заведением на стены 200 мм (по пирогу пола); тест проливом и акт скрытых работ
	Итого			**307,27**			**633,37**			**229,8**		**295,89**	

Допущения и предложения на листе

Основа листа: размеры и контуры этажей подобраны проектировщиком по составу помещений и площадям этажей с картинки 470 px (размеры на ней не читаются); обмер и исходный проект — задание (К-1); высоты: 1-й этаж 2800 мм, мансарда 2700 мм (горизонтальная часть) приняты; скаты кровли мансарды приняты по картинке: колено 1200 мм, уклон 45°, конёк вдоль длинной стороны; проект КР — задание (К-2); наружные стены 400 мм, перегородки 120 мм приняты (К-1); разрешённая мощность 15 кВт принята по типовым ТУ для частного дома (К-4); подрайон климата не задан — принят не северный (жилые от 2,5 м) (К-7).

Знак «**» — предложение проектировщика, заказчиком не утверждено (согласовать с заказчиком): записи в реестре нет: плинтус пом. 1, 2, 4–14, 16, 17, фартук пом. 1, акцент пом. 5 — артикул изделия не выбран: позиция описана характеристиками («аналог по характеристикам»), артикул выбирается при закупке; пол пом. 10 — покрытие пола гаража — предложение исполнителя: выдерживает шины, масло и антигололёдные реагенты, без швов.

См. лист открытых вопросов (лист 7, записи К-1, К-2, К-4, К-7).

Примечания

1. Площади поверхностей — по чистым граням стен до отделки: стены = периметр × высоту от чистого пола помещения до низа потолка минус проёмы (облицовка плиткой — до верха облицовки); плинтус = периметр минус дверные проёмы; пол и потолок — по площади помещения. Количество плиток по раскладке. Площади помещений — с учётом всех частей помещения; откосы в площадь стен не входят.
2. Акцентные стены и фартук — отдельными строками, их площадь вычтена из основной отделки стен помещения; фартук — над нижними модулями кухни от столешницы до низа навесных шкафов, где шкафов нет — на 600 мм.
3. Плинтус — длина по периметру за вычетом дверных проёмов; примыкания к наличникам и встроенной мебели — по развёрткам.
4. Формат плитки — Ш×В×Т (ширина × высота в положении укладки × толщина), мм; на полу — вдоль стен А/В × вдоль стен Б/Г.
5. Коды цвета — по веерам производителей; колеровка каждой краски одной партией, проверка выкраса при свете D65 и при лампах проекта.
6. Уровни подготовки Q1–Q4 — система Knauf, не норма ГОСТ/СП; допуски поверхностей — по СП 71.13330.2017 (действующая редакция).
7. «аналог:» — изделие задано характеристиками, марку и артикул согласовать с заказчиком до закупки.
8. Плавающая стяжка по звукоизоляции: демпферная (кромочная) лента по контуру помещения и у стояков (СП 51.13330.2011, п. 9.11); плинтус крепится только к стене.
9. Сводка площадей по материалам, м²: потолок — NCS S 0804-Y30R Luja 7 — 49,81; потолок — Little Greene No. 105 Anti-Reflex 2 — 202,86; потолок — Little Greene No. 105 Luja 7 — 20,86; потолок — NCS S 0804-Y30R Anti-Reflex 2 — 33,74; стены — NCS S 0804-Y30R Luja 7 — 113,38; стены — Farrow & Ball No. 226 Modern Emulsion — 325,94; стены — Farrow & Ball No. 298 Modern Emulsion — 5,68; стены — облицовка плиткой 600×1200×9 мм, Atlas Concorde A8UZ — 58,23; стены — NCS S 0804-Y30R Optiva 5 Matt — 32,20; стены — Farrow & Ball No. 93 Optiva 5 Matt — 12,92; стены — Little Greene No. 105 Harmony — 41,96; стены — NCS S 7020-G10Y Modern Emulsion — 7,60; стены — Farrow & Ball No. 64 Modern Emulsion 7,35; стены — NCS S 3020-G30Y Modern Emulsion — 12,33; стены — NCS S 3040-Y70R Modern Emulsion — 14,85; фартук — облицовка керамогранитом, #F1F1EC — 0,93.

Изм.	Кол.уч	Лист	№ док.	Подп.	Дата
Разраб.		Кырлан А.С.			21.10.26
Пров.					
ГИП					
Н. контр.					
Утв.					

ГД-2026-010-АИ

Дом 331 м²

Общая площадь 270,67* м² · * размеры приняты, не замерены (реестр — л. 7, К-1)

Дизайн-проект интерьера	Стадия	Лист	Листов
	РП	72	159

Ведомость отделки помещений. Лист 3 из 3

М б/м

Кырлан Александр Сергеевич

выпуск 18.10.2026 № 9365d64cec · стр. 76 из 197

Колерная карта

Цвета и материалы по помещениям · палитра проекта · лист 1 из 2

Колерная карта по помещениям

Помещение	Поверхность	Образец	Поз.	Система и код цвета	Производитель, линейка / материал, артикул	Блеск	Класс EN 13300	LRV	Площадь
1. Кухня-столовая 24,59 м²	стены		**К1**	NCS S 0804-Y30R	Tikkurila · Luja 7	полуматов.	1	85	45,0 м²
	потолок		**К2**	NCS S 0804-Y30R	Tikkurila · Luja 7	матовая	1	85	24,6 м²
	пол		**КМ1**	по образцу	Coswick · Вековые традиции				24,6 м²
	плинтус		**К3**	NCS S 0804-Y30R	МДФ · в цвет NCS	полуглянц.	2	85	18,3 м
	фартук		**КМ2**	тон Paper F497 (тёплый белый)	керамогранит · аналог по хар.				0,9 м²
2. Кабинет-гостевая 11,92 м²	стены		**К4**	Farrow & Ball No. 226	Farrow & Ball · Modern Emulsion	матовая	1	63	25,3 м²
	акцент А		**К5**	Farrow & Ball No. 298	Farrow & Ball · Modern Emulsion	матовая	1	14	5,7 м²
	потолок		**К6**	Little Greene No. 105	Tikkurila · Anti-Reflex 2	глубокомат.	2	82	11,9 м²
	пол		**КМ1**	по образцу	Coswick · Вековые традиции				11,9 м²
	плинтус		**К7**	Farrow & Ball No. 226	МДФ · в цвет Farrow & Ball			63	11,7 м
3. Санузел 1 этажа 4,87 м²	стены		**К8**	Atlas Concorde A8UZ	Atlas Concorde · Marvel Travertine				20,5 м²
	потолок		**К9**	Little Greene No. 105	Tikkurila · Luja 7	матовая	1	82	4,9 м²
	пол		**К8**	Atlas Concorde A8UZ	Atlas Concorde · Marvel Travertine				4,9 м²
4. Котельная 6,88 м²	стены		**К4**	Farrow & Ball No. 226	Farrow & Ball · Modern Emulsion	матовая	1	63	27,0 м²
	потолок		**К6**	Little Greene No. 105	Tikkurila · Anti-Reflex 2	глубокомат.	2	82	6,9 м²
	пол		**К8**	Atlas Concorde A8UZ	Atlas Concorde · Marvel Travertine				6,9 м²
	плинтус		**К7**	Farrow & Ball No. 226	МДФ · в цвет Farrow & Ball			63	9,7 м
5. Гостиная 33,74 м²	стены		**К10**	NCS S 0804-Y30R	Tikkurila · Optiva 5 Matt	матовая	2	85	32,2 м²
	акцент А		**К11**	Farrow & Ball No. 93	Tikkurila · Optiva 5 Matt	матовая	2	7	12,9 м²
	потолок		**К12**	NCS S 0804-Y30R	Tikkurila · Anti-Reflex 2	глубокомат.	2	85	33,7 м²
	пол		**КМ1**	по образцу	Coswick · Вековые традиции				33,7 м²
	плинтус		**К3**	NCS S 0804-Y30R	МДФ · в цвет NCS	полуглянц.	2	85	18,2 м
6. Холл с лестницей 10,02 м²	стены		**К4**	Farrow & Ball No. 226	Farrow & Ball · Modern Emulsion	матовая	1	63	22,3 м²
	потолок		**К6**	Little Greene No. 105	Tikkurila · Anti-Reflex 2	глубокомат.	2	82	10,0 м²
	пол		**КМ1**	по образцу	Coswick · Вековые традиции				10,0 м²
	плинтус		**К7**	Farrow & Ball No. 226	МДФ · в цвет Farrow & Ball			63	7,0 м
7. Кладовая 5,99 м²	стены		**К13**	Little Greene No. 105	Tikkurila · Harmony	матовая	1	82	23,3 м²
	потолок		**К6**	Little Greene No. 105	Tikkurila · Anti-Reflex 2	глубокомат.	2	82	6,0 м²
	пол		**КМ1**	по образцу	Coswick · Вековые традиции				6,0 м²
	плинтус		**К14**	Little Greene No. 105	МДФ · в цвет Little Greene			82	7,8 м
8. Прихожая 12,46 м²	стены		**К4**	Farrow & Ball No. 226	Farrow & Ball · Modern Emulsion	матовая	1	63	39,0 м²
	потолок		**К6**	Little Greene No. 105	Tikkurila · Anti-Reflex 2	глубокомат.	2	82	12,5 м²
	пол		**К8**	Atlas Concorde A8UZ	Atlas Concorde · Marvel Travertine				12,5 м²
	плинтус		**К7**	Farrow & Ball No. 226	МДФ · в цвет Farrow & Ball			63	13,6 м
9. Тамбур 3,49 м²	стены		**К4**	Farrow & Ball No. 226	Farrow & Ball · Modern Emulsion	матовая	1	63	17,1 м²
	потолок		**К6**	Little Greene No. 105	Tikkurila · Anti-Reflex 2	глубокомат.	2	82	3,5 м²
	пол		**К8**	Atlas Concorde A8UZ	Atlas Concorde · Marvel Travertine				3,5 м²
	плинтус		**К7**	Farrow & Ball No. 226	МДФ · в цвет Farrow & Ball			63	5,6 м
10. Гараж 41,58 м²	стены		**К4**	Farrow & Ball No. 226	Farrow & Ball · Modern Emulsion	матовая	1	63	62,6 м²
	потолок		**К6**	Little Greene No. 105	Tikkurila · Anti-Reflex 2	глубокомат.	2	82	41,6 м²
	пол		**КМ3**	по образцу	ероху · аналог по хар.				41,6 м²
	плинтус		**КМ4**	по образцу	pvc · аналог по хар.				22,0 м

Примечания

1. Цвет утверждается только по выкрасу на объекте: формат от А3 до 1000×1000 мм на загрунтованном ГКЛ, в 2 слоя (как на стене), не на белой шпаклёвке; смотреть днём и при свете проекта своего помещения, рядом с образцами пола и фасадов. Подпись на обороте: код, бренд и веер, дата.
2. Колеровка машинная в колеровочном центре бренда; каждый код — за один проход, одной партией на весь объём. Колеровщику передаётся только система и код утверждённого веера; плашки и HEX на листе — ориентир, печать не является эталоном цвета.
3. Класс мокрого истирания — EN 13300 (ISO 11998); блеск — по ГОСТ 31975 (ISO 2813), геометрия 60°. LRV — пересчёт координаты L* каталога производителя (Y = ((L*+16)/116)³); «≈» — расчёт по HEX, справочно.
4. Площади поверхностей — тем же способом и с теми же цифрами, что в ведомости отделки (способ счёта — в общих указаниях); объём краски к заказу, фасовка и материалы КМ — в спецификации отделочных материалов.
5. Колерная карта на 2 листах: обозначения повторены на каждом, схема квартиры и палитра — на первом, перечень выкрасов — на последнем.

Допущения и предложения на листе. Знак «**» предложено (согласовать): плинтус пом. 1, 2, 4–14, 16, 17, фартук пом. 1, акцент пом. 5, пол пом. 10. См. лист открытых вопросов (лист 7).

Схема палитры проекта

Стиль: Шале 60% + Эко и органический модерн 40% · схема: complement

основной	основной	основной	второстепенный	второстепенный	второстепенный	второстепенный	второстепенный	второстепенный	второстепенный	второстепенный	акцентный	акцентный	акцентный
Farrow & Ball No. 226	NCS S 0804-Y30R	Little Greene No. 105	Tikkurila V451	NCS S 3020-G30Y	Tikkurila X463	Farrow & Ball No. 226	Farrow & Ball No. 88	Farrow & Ball No. 240	NCS S 2005-Y20R	NCS S 3010-Y30R	NCS S 7020-G10Y	Farrow & Ball No. 64	Farrow & Ball No. 43
Joa's White LRV 63 стены 2,4,6,8,9,10,13,16,17,18,19; плинтус 3,4(без)5,6,7,8,10,11 (кроме фартука),12,15	тёплый молочный белый LRV 85 стены 1,5,11,12; потолок 1,5,11 (потолок 5 — после двух слоёв)	Slaked Lime LRV 82 потолок 2,3,4,5,7,8,9,10,11,12,13,15,16,17,18,19,20; стены 7 (в тамбуре)	Olive grove V451 LRV 51 текстиль/декор 18	шалфей LRV 38 акцент 18; текстиль/декор 17,18	Sandstone X463 LRV 51 текстиль/декор 2,16,19	Elephant's Ear — только для плинтусов LRV 52 текстиль/декор 13	Mouse's Ear — тёплый оттенок серого LRV 26 текстиль/декор 2	Charleston Grey — серо-оружейный графит LRV 30 текстиль/декор 5,10	Светлый песочно-серый LRV 60 текстиль/декор 1,5,13,18,19	орех/лён тёмный LRV 43 текстиль/декор 2,16,19	Хвойный тёмно-зелёный LRV ≈5 акцент 13; текстиль/декор 13	Red Earth LRV 18 акцент 16; текстиль/декор 16	Eating Room Red — бордовый серый LRV 11.8 в отделке не применён

План 60/30/10

Окраска, факт — по площади стен, акцентов, потолков

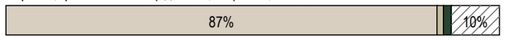

окрашено всего 939,7 м²; второстепенный тон несут мебель и текстиль

Условные обозначения

- **К1** NCS S 0804-Y30R · тёплый молочный белый · Tikkurila Luja 7 · полуматов. · кл. 1
- **К2** NCS S 0804-Y30R · тёплый молочный белый · Tikkurila Luja 7 · матовая · кл. 1
- **К3** NCS S 0804-Y30R · тёплый молочный белый · МДФ · полуглянц. · кл. 2
- **К4** Farrow & Ball No. 226 · Joa's White · Modern Emulsion · матовая · кл. 1
- **К5** Farrow & Ball No. 298 · Bancha · Modern Emulsion · матовая · кл. 1
- **К6** Little Greene No. 105 · Slaked Lime · Anti-Reflex 2 · глубокомат. · кл. 2
- **К7** Farrow & Ball No. 226 · Joa's White · МДФ
- **К8** Atlas Concorde A8UZ · Marvel Travertine · Marvel Travertine
- **К9** Little Greene No. 105 · Slaked Lime · Luja 7 · матовая · кл. 1
- **К10** NCS S 0804-Y30R · тёплый молочный белый · Tikkurila Optiva 5 Matt · матовая · кл. 2
- **К11** Farrow & Ball No. 93 · Studio Green — почти чёрный зелёный · Optiva 5 Matt · матовая · кл. 2
- **К12** NCS S 0804-Y30R · тёплый молочный белый · Tikkurila Anti-Reflex 2 · глубокомат. · кл. 2
- **К13** Little Greene No. 105 · Slaked Lime · Harmony · матовая · кл. 1
- **К14** Little Greene No. 105 · Slaked Lime · МДФ
- **К15** NCS S 7020-G10Y · Хвойный тёмно-зелёный · Farrow & Ball Modern Emulsion · матовая · кл. 1
- **К16** Farrow & Ball No. 64 · Red Earth · Modern Emulsion · матовая · кл. 1
- **К17** NCS S 3020-G30Y · шалфей · Farrow & Ball Modern Emulsion · матовая · кл. 1
- **К18** Farrow & Ball No. 226 · Joa's White · Contour (Luxxus)
- **К19** NCS S 3040-Y70R · обожжённая глина · Farrow & Ball Modern Emulsion · матовая · кл. 1
- **КМ1** инженерная доска · 1167-4250
- **КМ2** аналог: керамогранит матовый, тон F497, 600×600×9 мм
- **КМ3** ероху · аналог: наливной полимерный пол (эпоксидный), с кварцевой посыпкой, 3 мм
- **КМ4** pvc · аналог: плинтус ПВХ влагостойкий 100 мм, серый
- **КМ5** керамогранит · A8UZ
- **КМ6** керамогранит · аналог: плинтус из керамогранита пола, подрезка 80 мм, верхняя кромка с запилом 45°

дерево (доска, паркет, ламинат) — рисунок досок

керамогранит, плитка, камень — сетка швов по формату

материал без кода цвета — по образцу (артикул в ведомости отделки)

HEX не задан — цвет только по коду и вееру

К — позиция окраски (код + продукт + блеск), КМ — позиция материала, тон КМ — по описанию артикула, эталон — образец материала; ≈ LRV — расчёт по HEX, справочно

Изм.	Кол.уч	Лист	№ док.	Подп.	Дата
Разраб.		Кырлан А.С.			21.10.26
Пров.					
ГИП					
Н. контр.					
Утв.					

ГД-2026-010-АИ

Дом 331 м²

Общая площадь 270,67* м² · * размеры приняты, не замерены (реестр — л. 7, К-1)

Дизайн-проект интерьера

Стадия	Лист	Листов
РП	73	159

Колерная карта

М б/м

Кырлан Александр Сергеевич

выпуск 18.10.2026 № 9365d64cec · стр. 77 из 197

Колерная карта

Цвета и материалы по помещениям · выкрасы на согласование · лист 2 из 2

ПРЕДВАРИТЕЛЬНО · не для производства работ · открыто пунктов: 6 (реестр — л. 7)

Колерная карта по помещениям (продолжение)

Помещение	Поверхность	Образец	Поз.	Система и код цвета	Производитель, линейка / материал, артикул	Блеск	Класс EN 13300	LRV	Площадь
11. Веранда 21,84 м²	стены		**K1**	NCS S 0804-Y30R	Tikkurila · Luja 7	полуматов.	1	85	49,6 м²
	потолок		**K2**	NCS S 0804-Y30R	Tikkurila · Luja 7	матовая	1	85	21,8 м²
	пол		**KM5**	тон Claystone V486 (грейж)	Atlas Concorde · Marvel Travertine				21,8 м²
	плинтус		**KM6**	тон Claystone V486 (грейж)	керамогранит · аналог по хар.				20,5 м
12. Крыльцо 3,38 м²	стены		**K1**	NCS S 0804-Y30R	Tikkurila · Luja 7	полуматов.	1	85	18,7 м²
	потолок		**K2**	NCS S 0804-Y30R	Tikkurila · Luja 7	матовая	1	85	3,4 м²
	пол		**KM5**	тон Claystone V486 (грейж)	Atlas Concorde · Marvel Travertine				3,4 м²
	плинтус		**KM6**	тон Claystone V486 (грейж)	керамогранит · аналог по хар.				6,4 м
13. Спальня мастер 24,59 м²	стены		**K4**	Farrow & Ball No. 226	Farrow & Ball · Modern Emulsion	матовая	1	63	28,6 м²
	акцент А		**K15**	NCS S 7020-G10Y	Farrow & Ball · Modern Emulsion	матовая	1	≈5	7,6 м²
	потолок		**K6**	Little Greene No. 105	Tikkurila · Anti-Reflex 2	глубокомат.	2	82	27,1 м²
	пол		**KM1**	по образцу	Coswick · Вековые традиции				24,6 м²
	плинтус		**K7**	Farrow & Ball No. 226	МДФ · в цвет Farrow & Ball			63	18,7 м
14. Гардеробная мастер 6,74 м²	стены		**K13**	Little Greene No. 105	Tikkurila · Harmony	матовая	1	82	18,7 м²
	потолок		**K6**	Little Greene No. 105	Tikkurila · Anti-Reflex 2	глубокомат.	2	82	8,6 м²
	пол		**KM1**	по образцу	Coswick · Вековые традиции				6,7 м²
	плинтус		**K14**	Little Greene No. 105	МДФ · в цвет Little Greene			82	9,0 м
15. Санузел мастер 6,88 м²	стены		**K8**	Atlas Concorde A8UZ	Atlas Concorde · Marvel Travertine				19,9 м²
	потолок		**K9**	Little Greene No. 105	Tikkurila · Luja 7	матовая	1	82	7,8 м²
	пол		**K8**	Atlas Concorde A8UZ	Atlas Concorde · Marvel Travertine				6,9 м²
16. Спальня 2 15,52 м²	стены		**K4**	Farrow & Ball No. 226	Farrow & Ball · Modern Emulsion	матовая	1	63	28,1 м²
	акцент А		**K16**	Farrow & Ball No. 64	Farrow & Ball · Modern Emulsion	матовая	1	18	7,3 м²
	потолок		**K6**	Little Greene No. 105	Tikkurila · Anti-Reflex 2	глубокомат.	2	82	15,5 м²
	пол		**KM1**	по образцу	Coswick · Вековые традиции				15,5 м²
	плинтус		**K7**	Farrow & Ball No. 226	МДФ · в цвет Farrow & Ball			63	14,7 м
17. Холл мансарды 21,72 м²	стены		**K4**	Farrow & Ball No. 226	Farrow & Ball · Modern Emulsion	матовая	1	63	34,8 м²
	потолок		**K6**	Little Greene No. 105	Tikkurila · Anti-Reflex 2	глубокомат.	2	82	23,5 м²
	пол		**KM1**	по образцу	Coswick · Вековые традиции				21,7 м²
	плинтус		**K7**	Farrow & Ball No. 226	МДФ · в цвет Farrow & Ball			63	14,4 м
18. Спальня 3 17,11 м²	стены		**K4**	Farrow & Ball No. 226	Farrow & Ball · Modern Emulsion	матовая	1	63	25,5 м²
	акцент А		**K17**	NCS S 3020-G30Y	Farrow & Ball · Modern Emulsion	матовая	1	38	12,3 м²
	потолок		**K6**	Little Greene No. 105	Tikkurila · Anti-Reflex 2	глубокомат.	2	82	17,1 м²
	пол		**KM1**	по образцу	Coswick · Вековые традиции				17,1 м²
	плинтус		**K18**	Farrow & Ball No. 226	Orac Decor · Contour (Luxxus)			63	15,6 м
19. Спальня 4 16,28 м²	стены		**K4**	Farrow & Ball No. 226	Farrow & Ball · Modern Emulsion	матовая	1	63	15,8 м²
	акцент А		**K19**	NCS S 3040-Y70R	Farrow & Ball · Modern Emulsion	матовая	1	24	14,8 м²
	потолок		**K6**	Little Greene No. 105	Tikkurila · Anti-Reflex 2	глубокомат.	2	82	18,8 м²
	пол		**KM1**	по образцу	Coswick · Вековые традиции				16,3 м²
	плинтус		**K18**	Farrow & Ball No. 226	Orac Decor · Contour (Luxxus)			63	16,6 м
20. Санузел 2 6,29 м²	стены		**K8**	Atlas Concorde A8UZ	Atlas Concorde · Marvel Travertine				17,8 м²
	потолок		**K9**	Little Greene No. 105	Tikkurila · Luja 7	матовая	1	82	8,2 м²
	пол		**K8**	Atlas Concorde A8UZ	Atlas Concorde · Marvel Travertine				6,3 м²

Условные обозначения

- **K1** NCS S 0804-Y30R · тёплый молочный белый · Tikkurila Luja 7 · полуматов. · кл. 1
- **K2** NCS S 0804-Y30R · тёплый молочный белый · Tikkurila Luja 7 · матовая · кл. 1
- **K3** NCS S 0804-Y30R · тёплый молочный белый · МДФ · полуглянц. · кл. 2
- **K4** Farrow & Ball No. 226 · Joa's White · Modern Emulsion · матовая · кл. 1
- **K5** Farrow & Ball No. 298 · Bancha · Modern Emulsion · матовая · кл. 1
- **K6** Little Greene No. 105 · Slaked Lime · Anti-Reflex 2 · глубокомат. · кл. 2
- **K7** Farrow & Ball No. 226 · Joa's White · МДФ
- **K8** Atlas Concorde A8UZ · Marvel Travertine · Marvel Travertine
- **K9** Little Greene No. 105 · Slaked Lime · Luja 7 · матовая · кл. 1
- **K10** NCS S 0804-Y30R · тёплый молочный белый · Tikkurila Optiva 5 Matt · матовая · кл. 2
- **K11** Farrow & Ball No. 93 · Studio Green — почти чёрный зелёный · Optiva 5 Matt · матовая · кл. 2
- **K12** NCS S 0804-Y30R · тёплый молочный белый · Tikkurila Anti-Reflex 2 · глубокомат. · кл. 2
- **K13** Little Greene No. 105 · Slaked Lime · Harmony · матовая · кл. 1
- дерево (доска, паркет, ламинат) — рисунок досок
- керамогранит, плитка, камень — сетка швов по формату
- материал без кода цвета — по образцу (артикул в ведомости отделки)
- HEX не задан — цвет только по коду и вееру
- **K14** Little Greene No. 105 · Slaked Lime · МДФ
- **K15** NCS S 7020-G10Y · Хвойный тёмно-зелёный · Farrow & Ball Modern Emulsion · матовая · кл. 1
- **K16** Farrow & Ball No. 64 · Red Earth · Modern Emulsion · матовая · кл. 1
- **K17** NCS S 3020-G30Y · шалфей · Farrow & Ball Modern Emulsion · матовая · кл. 1
- **K18** Farrow & Ball No. 226 · Joa's White · Contour (Luxxus)
- **K19** NCS S 3040-Y70R · обожжённая глина · Farrow & Ball Modern Emulsion · матовая · кл. 1
- **KM1** инженерная доска · 1167-4250
- **KM2** аналог: керамогранит матовый, тон F497, 600×600×9 мм
- **KM3** epoxy · аналог: наливной полимерный пол (эпоксидный), с кварцевой посыпкой, 3 мм
- **KM4** pvc · аналог: плинтус ПВХ влагостойкий 100 мм, серый
- **KM5** керамогранит · A8UZ
- **KM6** керамогранит · аналог: плинтус из керамогранита пола, подрезка 80 мм, верхняя кромка с запилом 45°

Допущения и предложения на листе. Знак «**» предложено (согласовать): плинтус пом. 1, 2, 4–14, 16, 17, фартук пом. 1, акцент пом. 5, пол пом. 10. См. лист открытых вопросов (лист 7).

K — позиция окраски (код + продукт + блеск), KM — позиция материала, тон KM — по описанию артикула, эталон — образец материала; ≈ LRV — расчёт по HEX, справочно

Перечень выкрасов на согласование

№	Код	Бренд / веер	Пом. / стена	Подложка	Формат	Статус
1	S 0804-Y30R	NCS Tikkurila	1, 5, 11, 12	ГКЛ, загрунтованный под эту краску; МДФ, загрунтованный под эмаль	600×1000; 300×600	к выполнению
2	No. 226	Farrow & Ball	2, 4, 6, 8, 9, 10, 13, 16, 17, 18, 19	ГКЛ, загрунтованный под эту краску; МДФ, загрунтованный под эмаль	600×1000; 300×600	к выполнению
3	No. 298	Farrow & Ball	2 A	ГКЛ, загрунтованный под эту краску	600×1000	к выполнению
4	No. 105	Little Greene	2, 3, 4, 6, 7, 8, 9, 10, 13, 14, 15, 16, 17, 18, 19, 20	ГКЛ, загрунтованный под эту краску; МДФ, загрунтованный под эмаль	600×1000; 300×600	к выполнению
5	No. 93	Farrow & Ball	5 A	ГКЛ, загрунтованный под эту краску	600×1000	к выполнению
6	S 7020-G10Y	NCS Farrow & Ball	13 A	ГКЛ, загрунтованный под эту краску	600×1000	к выполнению
7	No. 64	Farrow & Ball	16 A	ГКЛ, загрунтованный под эту краску	600×1000	к выполнению

… ещё 2 выкрасов — в ведомости отделки

Примечания

1. Цвет утверждается только по выкрасу на объекте: формат от А3 до 1000×1000 мм на загрунтованном ГКЛ, в 2 слоя (как на стене), не на белой шпаклёвке; смотреть днём и при свете проекта своего помещения, рядом с образцами пола и фасадов. Подпись на обороте: код, бренд и веер, дата.
2. Колеровка машинная в колеровочном центре бренда; каждый код — за один проход, одной партией на весь объём. Колеровщику передаётся только система и код утверждённого веера; плашки и HEX на листе — ориентир, печать не является эталоном цвета.
3. Класс мокрого истирания — EN 13300 (ISO 11998); блеск — по ГОСТ 31975 (ISO 2813), геометрия 60°. LRV — пересчёт координаты L* каталога производителя ($Y = ((L^*+16)/116)^3$); «≈» — расчёт по HEX, справочно.
4. Площади поверхностей — тем же способом и с теми же цифрами, что в ведомости отделки (способ счёта — в общих указаниях); объём краски к заказу, фасовка и материалы КМ — в спецификации отделочных материалов.
5. Перечень выкрасов составлен по кодам колерной карты; к основному тону стен добавить на выкрас 2 соседних тона того же веера (светлее и темнее), статус отмечать в графе «Статус» при согласовании.
6. Колерная карта на 2 листах: обозначения повторены на каждом, схема квартиры и палитра — на первом, перечень выкрасов — на последнем.

Изм.	Кол.уч	Лист	№ док.	Подп.	Дата
Разраб.		Кырлан А.С.			21.10.26
Пров.					
ГИП					
Н. контр.					
Утв.					

ГД-2026-010-АИ

Дом 331 м²

Общая площадь 270,67* м² · * размеры приняты, не замерены (реестр — л. 7, К-1)

Дизайн-проект интерьера

Стадия	Лист	Листов
РП	74	159

Колерная карта

М б/м

Кырлан Александр Сергеевич

выпуск 18.10.2026 № 9365d64cec · стр. 78 из 197

Спецификация отделочных материалов

ПРЕДВАРИТЕЛЬНО · не для производства работ · открыто пунктов: 6 (реестр — л. 7)

Форма 1 по ГОСТ 21.110-2013 · количества — из геометрии проекта, с запасом · часть 1 из 2

Поз.	Наименование и техническая характеристика	Тип, марка, обозначение документа	Код продукции	Поставщик	Ед. изм.	Кол.	Масса 1 ед., кг	Примечание
	Лакокрасочные материалы							
1	Краска интерьерная водно-дисперсионная акриловая для стен, полуматовая, класс мокрого истирания 1 по EN 13300, база A; цвет NCS S 0804-Y30R «S 0804-Y30R», колеровка машинная	Tikkurila Luja 7		Tikkurila	л	30,6		поз. К1 колерной карты; пом. 1, 11, 12; S = 113,4 м² × 2 сл. × 0,12 л/м² = 27,2 л, +10 % и 0,5 л на подкраску → ≥ 30,4 л; тара 3 × 9 л + 1 × 2,7 л + 1 × 0,9 л
2	Краска интерьерная водно-дисперсионная акриловая для потолков, матовая, класс мокрого истирания 1 по EN 13300, база A; цвет NCS S 0804-Y30R «S 0804-Y30R», колеровка машинная	Tikkurila Luja 7		Tikkurila	л	14,4		поз. К2 колерной карты; пом. 1, 11, 12; S = 49,8 м² × 2 сл. × 0,12 л/м² = 12,0 л, +10 % и 0,5 л на подкраску → ≥ 13,6 л; тара 1 × 9 л + 2 × 2,7 л
3	Краска интерьерная водно-дисперсионная акриловая для стен, матовая, класс мокрого истирания 1 по EN 13300, база A; цвет Farrow & Ball No. 226 «Joa's White», колеровка машинная	Farrow & Ball Modern Emulsion		Farrow & Ball	л	87,5		поз. К4 колерной карты; пом. 2, 4, 6, 8, 9, 10, 13, 16, 17, 18, 19; S = 325,9 м² × 2 сл. × 0,12 л/м² = 78,2 л, +10 % и 0,5 л на подкраску → ≥ 86,5 л; тара 17 × 5 л + 1 × 2,5 л
4	Краска интерьерная водно-дисперсионная акриловая для акцентных стен, матовая, класс мокрого истирания 1 по EN 13300, база C; цвет Farrow & Ball No. 298 «Bancha», колеровка машинная	Farrow & Ball Modern Emulsion		Farrow & Ball	л	2,5		поз. К5 колерной карты; пом. 2; S = 5,7 м² × 2 сл. × 0,12 л/м² = 1,4 л, +10 % и 0,5 л на подкраску → ≥ 2,0 л; тара 1 × 2,5 л
5	Краска интерьерная водно-дисперсионная акриловая для потолков, глубокоматовая, класс мокрого истирания 2 по EN 13300, база A; цвет Little Greene No. 105 «Slaked Lime», колеровка машинная	Tikkurila Anti-Reflex 2		Tikkurila	л	54,9		поз. К6 колерной карты; пом. 2, 4, 6, 7, 8, 9, 10, 13, 14, 16, 17, 18, 19; S = 202,9 м² × 2 сл. × 0,12 л/м² = 48,7 л, +10 % и 0,5 л на подкраску → ≥ 54,1 л; тара 6 × 9 л + 1 × 0,9 л
6	Краска интерьерная водно-дисперсионная акриловая для потолков, матовая, класс мокрого истирания 1 по EN 13300, база A; цвет Little Greene No. 105 «Slaked Lime», колеровка машинная	Tikkurila Luja 7		Tikkurila	л	6,3		поз. К9 колерной карты; пом. 3, 15, 20; S = 20,9 м² × 2 сл. × 0,12 л/м² = 5,0 л, +10 % и 0,5 л на подкраску → ≥ 6,0 л; тара 2 × 2,7 л + 1 × 0,9 л
7	Краска интерьерная водно-дисперсионная акриловая для стен, матовая, класс мокрого истирания 2 по EN 13300, база A; цвет NCS S 0804-Y30R «S 0804-Y30R», колеровка машинная	Tikkurila Optiva 5 Matt		Tikkurila	л	9,9		поз. К10 колерной карты; пом. 5; S = 32,2 м² × 2 сл. × 0,12 л/м² = 7,7 л, +10 % и 0,5 л на подкраску → ≥ 9,0 л; тара 1 × 9 л + 1 × 0,9 л
8	Краска интерьерная водно-дисперсионная акриловая для акцентных стен, матовая, класс мокрого истирания 2 по EN 13300, база C; цвет Farrow & Ball No. 93 «Studio Green — почти чёрный зелёный», колеровка машинная	Tikkurila Optiva 5 Matt		Tikkurila	л	7,5		поз. К11 колерной карты; пом. 5; S = 12,9 м² × 3 сл. × 0,12 л/м² = 4,7 л, +10 % и 0,5 л на подкраску → ≥ 5,6 л; тара 1 × 5 л + 1 × 2,5 л
9	Краска интерьерная водно-дисперсионная акриловая для потолков, глубокоматовая, класс мокрого истирания 2 по EN 13300, база A; цвет NCS S 0804-Y30R «S 0804-Y30R», колеровка машинная	Tikkurila Anti-Reflex 2		Tikkurila	л	9,9		поз. К12 колерной карты; пом. 5; S = 33,7 м² × 2 сл. × 0,12 л/м² = 8,1 л, +10 % и 0,5 л на подкраску → ≥ 9,4 л; тара 1 × 9 л + 1 × 0,9 л
10	Краска интерьерная водно-дисперсионная акриловая для стен, матовая, класс мокрого истирания 1 по EN 13300, база A; цвет Little Greene No. 105 «Slaked Lime», колеровка машинная	Tikkurila Harmony		Tikkurila	л	11,7		поз. К13 колерной карты; пом. 7, 14; S = 42,0 м² × 2 сл. × 0,12 л/м² = 10,1 л, +10 % и 0,5 л на подкраску → ≥ 11,6 л; тара 1 × 9 л + 1 × 2,7 л
11	Краска интерьерная водно-дисперсионная акриловая для акцентных стен, матовая, класс мокрого истирания 1 по EN 13300, база C; цвет NCS S 7020-G10Y «Хвойный тёмно-зелёный», колеровка машинная	Farrow & Ball Modern Emulsion		Farrow & Ball	л	5		поз. К15 колерной карты; пом. 13; S = 7,6 м² × 2 сл. × 0,12 л/м² = 1,8 л, +10 % и 0,5 л на подкраску → ≥ 2,5 л; тара 1 × 5 л
12	Краска интерьерная водно-дисперсионная акриловая для акцентных стен, матовая, класс мокрого истирания 1 по EN 13300, база C; цвет Farrow & Ball No. 64 «Red Earth», колеровка машинная	Farrow & Ball Modern Emulsion		Farrow & Ball	л	2,5		поз. К16 колерной карты; пом. 16; S = 7,3 м² × 2 сл. × 0,12 л/м² = 1,8 л, +10 % и 0,5 л на подкраску → ≥ 2,4 л; тара 1 × 2,5 л
13	Краска интерьерная водно-дисперсионная акриловая для акцентных стен, матовая, класс мокрого истирания 1 по EN 13300, база C; цвет NCS S 3020-G30Y «S 3020-G30Y», колеровка машинная	Farrow & Ball Modern Emulsion		Farrow & Ball	л	5		поз. К17 колерной карты; пом. 18; S = 12,3 м² × 2 сл. × 0,12 л/м² = 3,0 л, +10 % и 0,5 л на подкраску → ≥ 3,8 л; тара 1 × 5 л
14	Краска интерьерная водно-дисперсионная акриловая для акцентных стен, матовая, класс мокрого истирания 1 по EN 13300, база C; цвет NCS S 3040-Y70R «S 3040-Y70R», колеровка машинная	Farrow & Ball Modern Emulsion		Farrow & Ball	л	5		поз. К19 колерной карты; пом. 19; S = 14,8 м² × 2 сл. × 0,12 л/м² = 3,6 л, +10 % и 0,5 л на подкраску → ≥ 4,4 л; тара 1 × 5 л
15	Акрилово-уретановая эмаль на водной основе, полуглянцевая в цвет NCS S 0804-Y30R «S 0804-Y30R» — окраска плинтуса	аналог по характеристикам			л	1		поз. К3; пом. 1, 5; L = 36,5 м, S = 3,5 м² × 2 сл. × 0,12 л/м² + 10 %; продукт подобрать в веере NCS
16	Краска для МДФ и дерева в цвет Farrow & Ball No. 226 «Joa's White» — окраска плинтуса; блеск не ниже блеска стен	марка не задана			л	3,2		поз. К7, К18; пом. 2, 4, 6, 8, 9, 13, 16, 17, 18, 19; L = 127,7 м, S = 11,9 м² × 2 сл. × 0,12 л/м² + 10 %; продукт подобрать в веере Farrow & Ball
17	Краска для МДФ и дерева в цвет Little Greene No. 105 «Slaked Lime» — окраска плинтуса; блеск не ниже блеска стен	марка не задана			л	0,5		поз. К14; пом. 7, 14; L = 16,8 м, S = 1,6 м² × 2 сл. × 0,12 л/м² + 10 %; продукт подобрать в веере Little Greene
18	Грунтовка акриловая под окраску стен и потолков — из системы производителя краски	по системе краски			м²	882		площадь окраски стен, акцентов и потолков; 1 слой перед окраской; расход — по ТУ грунтовки

Допущения и предложения на листе

Основа листа: размеры и контуры этажей подобраны проектировщиком по составу помещений и площадям этажей с картинки 470 px (размеры на ней не читаются); обмер и исходный проект — задание (К-1); высоты: 1-й этаж 2800 мм, мансарда 2700 мм (горизонтальная часть) приняты; скаты кровли мансарды приняты по картинке: колено 1200 мм, уклон 45°, конёк вдоль длинной стороны; проект КР — задание (К-2); наружные стены 400 мм, перегородки 120 мм приняты (К-1); разрешённая мощность 15 кВт принята по типовым ТУ для частного дома (К-4); подрайон климата не задан — принят не северный (жилые от 2,5 м) (К-7).

Знак «**» — предложение проектировщика, заказчиком не утверждено (согласовать с заказчиком): записи в реестре нет: плинтус пом. 1, 2, 4–14, 16, 17, фартук пом. 1, акцент пом. 5 — артикул изделия не выбран: позиция описана характеристиками («аналог по характеристикам»), артикул выбирается при закупке; пол пом. 10 — покрытие пола гаража — предложение исполнителя: выдерживает шины, масло и антигололёдные реагенты, без швов.

См. лист открытых вопросов (лист 7, записи К-1, К-2, К-4, К-7).

Изм.	Кол.уч	Лист	№ док.	Подп.	Дата
Разраб.		Кырлан А.С.			21.10.26
Пров.					
ГИП					
Н. контр.					
Утв.					

ГД-2026-010-АИ

Дом 331 м²

Общая площадь 270,67* м² · * размеры приняты, не замерены (реестр — л. 7, К-1)

Дизайн-проект интерьера	Стадия	Лист	Листов
	РП	75	159
Спецификация отделочных материалов М б/м	**Кырлан Александр Сергеевич**		

Спецификация отделочных материалов

ПРЕДВАРИТЕЛЬНО · не для производства работ · открыто пунктов: 6 (реестр — л. 7)

Форма 1 по ГОСТ 21.110-2013 · количества — из геометрии проекта, с запасом · часть 2 из 2

Поз.	Наименование и техническая характеристика	Тип, марка, обозначение документа	Код продукции	Поставщик	Ед. изм.	Кол.	Масса 1 ед., кг	Примечание
	Плитка и керамогранит							
19	Керамогранит под травертин, 600×600 мм	аналог по характеристикам			м²	21,24		шов 2 мм; Санузел 1 этажа, пол; Санузел мастер, пол; Санузел 2, пол; по раскладке 53 шт (S = 18,04 м²), с запасом 59 шт
20	Керамогранит под травертин, 600×1200×9 мм, ректификат, водопоглощение 0,1 %	аналог по характеристикам		Atlas Concorde	м²	94,32		шов 2 мм; Санузел 1 этажа, стены А–Г; Санузел 1 этажа, короб инсталляции; Санузел мастер, стены А–Г; Санузел мастер, короб инсталляции; Санузел 2, стены А–Г; Санузел 2, короб инсталляции; по раскладке 116 шт (S = 60,56 м²), с запасом 131 шт
21	A8UZ, 600×1200×9 мм, ректификат, водопоглощение 0,1 % (BIa), противоскольжение R10, PEI IV	A8UZ		Atlas Concorde	м²	66,24		шов 2 мм; Котельная, пол; Прихожая, пол; Тамбур, пол; Веранда, пол; Крыльцо, пол; по раскладке 82 шт (S = 48,05 м²), с запасом 92 шт
22	Керамогранит матовый, тон F497, ректификат, водопоглощение 0,5 % (BIa)	аналог по характеристикам			м²	1,02		1. Кухня-столовая, фартук; раскладка не выполнена — S = 0,93 м² + 10 %; клей и затирка — по раскладке
23	Плинтус из керамогранита пола, подрезка 80 мм, верхняя кромка с запилом 45°	аналог по характеристикам			м²	22,53		11. Веранда, стены; раскладка не выполнена — S = 20,48 м² + 10 %; клей и затирка — по раскладке
24	Плинтус из керамогранита пола, подрезка 80 мм, верхняя кромка с запилом 45°	аналог по характеристикам			м²	7		12. Крыльцо, стены; раскладка не выполнена — S = 6,36 м² + 10 %; клей и затирка — по раскладке
	Напольные покрытия							
25	1167-4250, рабочий слой 4 мм, эмиссия E1, укладка на клей	1167-4250		Coswick	м²	201,4		пом. 1, 2, 5, 6, 7, 13, 14, 16, 17, 18, 19; S = 188,22 м² + 7 % (прямая укладка); к заказу — кратно упаковке
26	Клей для паркета и инженерной доски, эластичный (СМП / полиуретановый)	по рекомендации производителя доски			м²	189		площадь приклейки; расход и шпатель — по ТУ клея
	Погонажные изделия							
27	Плинтус МДФ под окраску 80×16 мм, крепление к стене, окраска в цвет NCS S 0804-Y30R	аналог по характеристикам			м	41		пом. 1, 5; L = 36,5 м (периметр без дверных проёмов) + 10 % на подрезку; в штуках — по длине планки
28	Плинтус МДФ под покраску 80×16, крепление к стене, окраска в цвет Farrow & Ball No. 226	аналог по характеристикам			м	124		пом. 2, 4, 6, 7, 8, 9, 13, 14, 16, 17; L = 112,3 м (периметр без дверных проёмов) + 10 % на подрезку; в штуках — по длине планки
29	Плинтус ПВХ влагостойкий 100 мм, серый, h = 100 мм, крепление к стене	аналог по характеристикам			м	25		пом. 10; L = 22,0 м (периметр без дверных проёмов) + 10 % на подрезку; в штуках — по длине планки
30	Плинтус из керамогранита пола, подрезка 80 мм, верхняя кромка с запилом 45°, h = 80 мм, крепление к стене	аналог по характеристикам			м	30		пом. 11, 12; L = 26,8 м (периметр без дверных проёмов) + 10 % на подрезку; в штуках — по длине планки
31	SX165, h = 69 мм, крепление к стене, окраска в цвет Farrow & Ball No. 226	SX165		Orac Decor	м	36		пом. 18, 19; L = 32,2 м (периметр без дверных проёмов) + 10 % на подрезку; в штуках — по длине планки
	Смеси и материалы для облицовки							
32	Затирка для швов плитки, класс CG2WA по EN 13888	Mapei Ultracolor Plus 132		Mapei	кг	10,7		по раскладке (a+b)/(a·b) × шов × t × 1,6 + 10 %; в т. ч. 3,8 кг — позиции раскладки без марки
33	Клей плиточный C2 TE S1 по EN 12004, слой 5 мм	Ceresit CM 17		Ceresit	кг	1052		43 меш. по 25 кг; 1,5 кг/м² на 1 мм слоя + 10 %; в т. ч. 370 кг — позиции раскладки без марки
34	Гидроизоляция обмазочная мокрых зон: пол, стены по периметру, зоны замачивания; 2 слоя с армирующей лентой в углах	аналог по характеристикам			м²	43,1		площадь по листу раскладки плитки + 10 %; расход смеси — по ТУ
35	Лента демпферная по периметру пола из плитки	аналог по характеристикам			м	85,5		периметр без дверных проёмов + 10 %

Примечания

1. Количества — из геометрии проекта: площади поверхностей по чистым граням стен до отделки (те же, что в ведомости отделки и колерной карте), плитка, клей и затирка — по раскладке плиточника; в графе «Кол.» — к заказу, с запасом.
2. Краска: расход 0,12 л/м² на слой в 2 слоя, если по ТУ не задан иной; запас 10 % и 0,5 л на подкраску каждого кода. Один код — одна партия, колеровка машинная в колеровочном центре бренда; в заказ — только после утверждения выкраса (колерная карта). Фасовка — по каталогу бренда на дату выпуска; к заказу — не меньше расчётного объёма.
3. «Аналог по характеристикам» — допускается изделие другого производителя с характеристиками не ниже указанных, по согласованию с автором проекта.
4. Графы «Код продукции» и «Масса 1 ед.» не заполнены: коды по классификатору продукции не присвоены, масса единицы до 25 кг (ГОСТ 21.110-2013).
5. Грунтовка и клей для доски указаны площадью обработки; объём — по ТУ выбранного продукта.

Допущения и предложения на листе

Основа листа: размеры и контуры этажей подобраны проектировщиком по составу помещений и площадям этажей с картинки 470 px (размеры на ней не читаются); обмер и исходный проект — задание (К-1); высоты: 1-й этаж 2800 мм, мансарда 2700 мм (горизонтальная часть) приняты; скаты кровли мансарды приняты по картинке: колено 1200 мм, уклон 45°, конёк вдоль длинной стороны; проект КР — задание (К-2); наружные стены 400 мм, перегородки 120 мм приняты (К-1); разрешённая мощность 15 кВт принята по типовым ТУ для частного дома (К-4); подрайон климата не задан — принят не северный (жилые от 2,5 м) (К-7).

Знак «**» — предложение проектировщика, заказчиком не утверждено (согласовать с заказчиком): записи в реестре нет: плинтус пом. 1, 2, 4–14, 16, 17, фартук пом. 1, акцент пом. 5 — артикул изделия не выбран: позиция описана характеристиками («аналог по характеристикам»), артикул выбирается при закупке; пол пом. 10 — покрытие пола гаража — предложение исполнителя: выдерживает шины, масло и антигололёдные реагенты, без швов.

См. лист открытых вопросов (лист 7, записи К-1, К-2, К-4, К-7).

Изм.	Кол.уч	Лист	№ док.	Подп.	Дата
Разраб.		Кырлан А.С.			21.10.26
Пров.					
ГИП					
Н. контр.					
Утв.					

ГД-2026-010-АИ

Дом 331 м²

Общая площадь 270,67* м² · * размеры приняты, не замерены (реестр — л. 7, К-1)

Дизайн-проект интерьера

Стадия	Лист	Листов
РП	76	159

Спецификация отделочных материалов

М б/м

Кырлан Александр Сергеевич

Концепция декора и визуализации

Шале · визуализации, палитра, материалы, ключевые предметы

Визуализация 1. Вид сверху (3D): планировка с мебелью, текстилем и декором

Расстановка — по плану мебели (лист 24); шторы, ковры, картины и растения — по плану текстиля и декора (лист 78).

Визуализация 22. Гостиная (пом. 5)

шторы Т1, Т2 · ковёр Т3 · картина ДК1 · растение ДК2, ДК21 · подушки, пледы Т4, Т5, Т6

Визуализация 20. Кухня-столовая (пом. 1)

шторы Т14 · растение ДК9

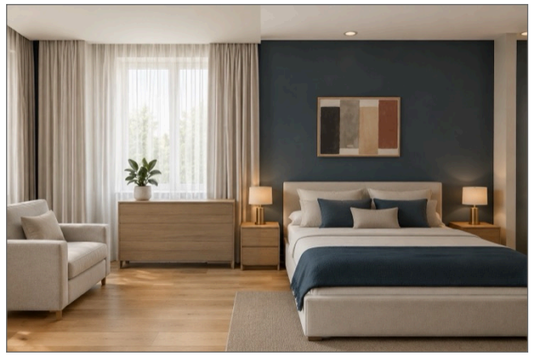

Визуализация 8. Спальня мастер (пом. 13)

шторы Т13, Т15 · ковёр Т16 · картина ДК4 · растение ДК27 · подушки, пледы Т17, Т18, Т19

Визуализация 10. Спальня 2 (пом. 16)

шторы Т20, Т21 · ковёр Т22 · картина ДК6 · зеркало ДК7 · подушки, пледы Т23, Т24, Т25

Материалы и фактуры

Дуб натуральный

пол: пом. 1, 2, 5, 6, 7, 13, 14, 16, 17, 18, 19; рамы ДК3, ДК4,

Букле

подушки: Т10, Т23, Т29, Т35

Лён

рулонная, портьеры, подушки: Т1, Т4, Т14, Т20, Т26, Т32, Т40, Т41

Бронза и чёрный металл

рамы ДК5, ДК7, ДК11, ДК13 чёрный; фурнитура, светильники

Бархат

подушки: Т5, Т11, Т18, Т24, Т30, Т36

Ключевые предметы

— Диван Кб3 2000×900 — кабинет-гостевая; подушки и плед Т10, Т11, Т12
— Диван Гс2 3200×1000 — гостиная; подушки и плед Т4, Т5, Т6
— Диван Вр2 2000×800 — веранда
— Кровати Д1, Д4, М1, С1 — над изголовьем картины ДК4, ДК6, ДК10, ДК12; текстиль Т17, Т18, Т19, Т23, Т24, Т25, Т29, Т30, Т31, Т35, Т36, Т37
— Ковры Т3, Т9, Т16, Т22, Т28, Т34, Т40, Т41 — джут плетёный, шерсть с джутом, резиновая крошка SBR с цветными EPDM-вкраплениями, шерсть, TPE, хлопок
— Картины ДК1, ДК3, ДК4, ДК6, ДК10, ДК12 — центр на высоте 1450–1650 мм
— Зеркала в рост ДК5, ДК7, ДК11, ДК31; над умывальниками ДК13
— Шторы-волна Т1, Т7, Т13, Т20, Т26, Т32 (Farrow & Ball No. 40), тюль Т2, Т8, Т15, Т21, Т27, Т33 (NCS S 0804-Y30R) — в нишах потолка

Настроение

Современное шале 60 % + эко (eco-organic.json) 40 %: загородный дом у леса. Стены — шерстяной белый Joa's White No. 226 и молочный S 0804-Y30R, потолки — известковый Slaked Lime No. 105; второй план — выцветший оливковый V451, шалфей S 3020-G30Y, песчаник X463; акценты — хвойный S 7020-G10Y, терракота Red Earth No. 64, брусника Eating Room Red No. 43. Дерево — дуб и лиственница под маслом, камень у камина. Настроение стиля: защищённый, тёплый, основательный, природный, камерный, после мороза — у огня. Свет тёплый, 2200–2700 K.

Примечания

1. Визуализации — образ интерьера. Изделия, размеры, высоты подвеса и привязки — по чертежам (план текстиля и декора — лист 78; шторы и карнизы — лист 80; ведомость текстиля — лист 81; ведомость декора и развеска — лист 83); при расхождении действуют чертежи и ведомости.
2. Коды цвета — ориентир подбора по веерам производителей; ткань утверждается по образцу при дневном свете и при свете проекта 2700–3000 K.
3. Мелкий стайлинг на визуализациях (книги, посуда, свечи) в ведомости не входит и поставляется заказчиком по желанию.

Палитра 60/30/10 и цвета текстиля

- Farrow & Ball No. 226 (Joa's White), LRV 63 — 60 % база — Т4, Т33
- Little Greene No. 105 (Slaked Lime), LRV 82 — 60 % база — Т15, Т21
- NCS S 3020-G30Y (шалфей), LRV 38 — 30 % второй цвет — Т30, Т31, Т41
- Farrow & Ball No. 229 (Elephant's Breath — тёплый средне-серый с лиловым подтоном), LRV 52 — 30 % второй цвет — Т13
- Farrow & Ball No. 243 (Charleston Gray — серо-коричневый «камень»), LRV 30 — 30 % второй цвет — Т3, Т40
- NCS S 0804-Y30R (тёплый молочный белый), LRV 85 — 60 % база — Т2, Т8, Т27
- Tikkurila V451 (выцветший оливковый), LRV 51 — 30 % второй цвет — Т26, Т29
- Tikkurila X463 (бежевый песчаник), LRV 51 — 30 % второй цвет — Т9, Т20, Т23, Т35
- Farrow & Ball No. 40 (Mouse's Back — тёплый коричнево-серый), LRV 26 — 30 % второй цвет — Т7
- NCS S 2005-Y20R (Светлый песочно-серый), LRV 60 — 30 % второй цвет — Т1, Т14, Т16, Т17, Т28, Т32

Допущения и предложения на листе. Основа листа: размеры и контуры этажей подобраны проектировщиком по составу помещений и площадям этажей с картинки 470 px (размеры на ней не читаются); обмер и исходный проект — задание (К-1); высоты: 1-й этаж 2800 мм, мансарда 2700 мм (горизонтальная часть) приняты; скаты кровли мансарды приняты по картинке: колено 1200 мм, уклон 45°, конёк вдоль длинной стороны; проект КР — задание (К-2); наружные стены 400 мм, перегородки 120 мм приняты (К-1); разрешённая мощность 15 кВт принята по типовым ТУ для частного дома (К-4); подрайон климата не задан — принят не северный (жилые от 2,5 м) (К-7). См. лист открытых вопросов (лист 7, записи К-1, К-2, К-4, К-7).

Изм.	Кол.уч	Лист	№ док.	Подп.	Дата
Разраб.		Кырлан А.С.			21.10.26
Пров.					
ГИП					
Н. контр.					
Утв.					

ГД-2026-010-АИ

Дом 331 м²

Общая площадь 270,67* м² · * размеры приняты, не замерены (реестр — л. 7, К-1)

Дизайн-проект интерьера

Стадия	Лист	Листов
РП	77	159

Концепция декора и визуализации

М б/м

Кырлан Александр Сергеевич

выпуск 18.10.2026 № 9365d64cec · стр. 81 из 197

План текстиля и декора · 1-й этаж

Шторы и карнизы, ковры, картины и зеркала, растения · размеры в мм от чистовых стен и чистого пола · марки — по ведомостям

ПРЕДВАРИТЕЛЬНО · не для производства работ · открыто пунктов: 6 (реестр — л. 7)

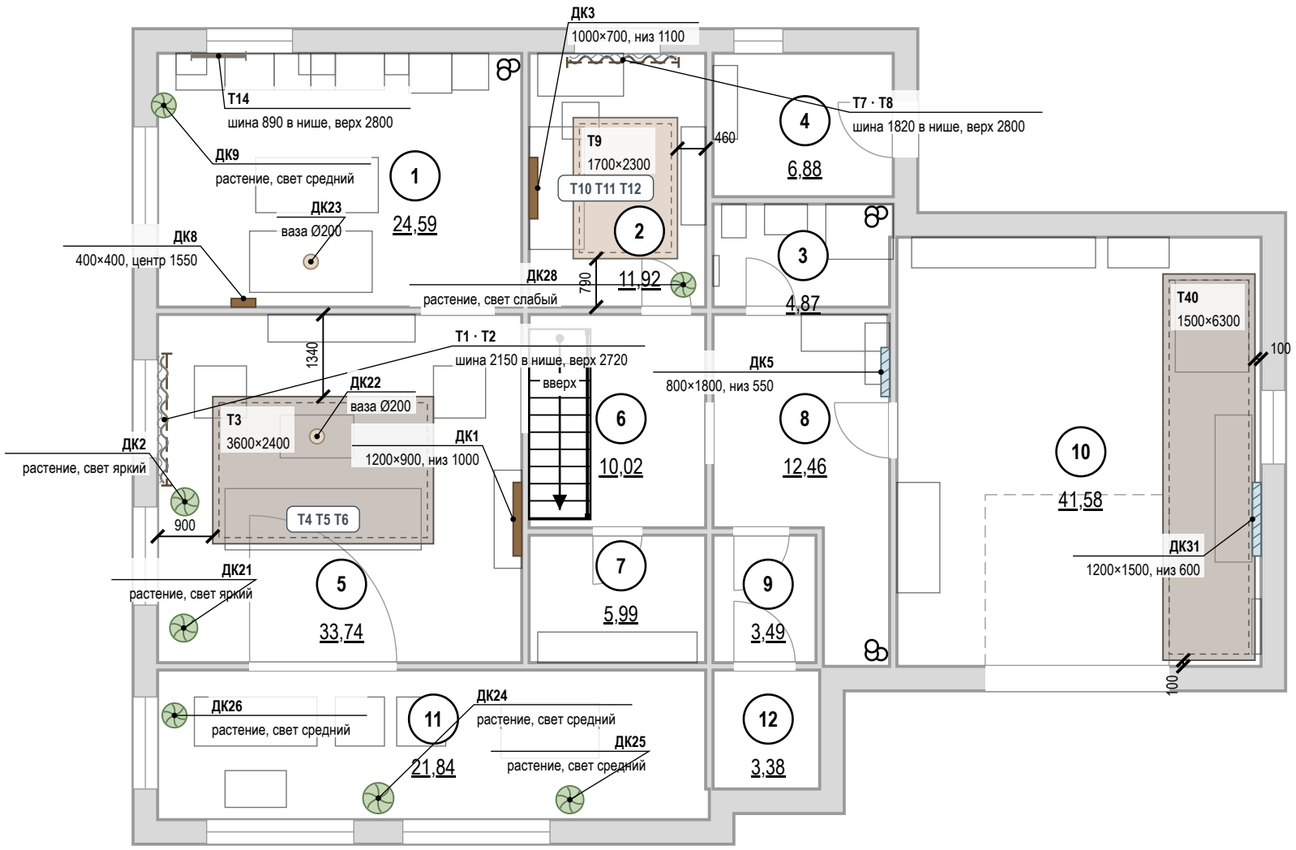

Условные обозначения

- ковёр — габарит в масштабе, цвет изделия
- шина или карниз штор (выше плоскости разреза)
- портьеры (штора-волна)
- тюль (на плане — волнистая линия)
- римская или рулонная штора в проёме
- картина на стене — ширина в масштабе
- зеркало на стене — ширина в масштабе
- растение в кашпо — диаметр в масштабе
- ваза, настольный декор
- подушки, пледы — марки на мебели
- привязка от чистовой стены, мм
- (1) номер помещения, площадь м²
- стены (подложка обмера)

Т1, ДК1 — марки по ведомостям текстиля и декора

Экспликация помещений

лист 15 · на плане — номера в марках

Окна: шина → полотно, мм

Поз.	Шина	Верх шины	Полотно, низ
Т14	890	2800, ниша	2000, низ 800
Т7, Т8	1820	2800, ниша	2790, низ 10
Т1, Т2	2150	2720, ниша	2710, низ 10

Развеска: высоты от пола, мм

Поз.	Пом.	Ш×В	Центр	Низ	Стена
ДК1	5	1200×900	1450	1000	Б
ДК3	2	1000×700	1450	1100	Г
ДК5	8	800×1800	1450	550	Б
ДК8	1	400×400	1550	1350	В
ДК31	10	1200×1500	1350	600	Б

Допущения и предложения на листе

Основа листа: размеры и контуры этажей подобраны проектировщиком по составу помещений и площадям этажей с картинки 470 px (размеры на ней не читаются); обмер и исходный проект — задание (К-1); высоты: 1-й этаж 2800 мм, мансарда 2700 мм (горизонтальная часть) приняты; скаты кровли мансарды приняты по картинке: колено 1200 мм, уклон 45°, конёк вдоль длинной стороны; проект КР — задание (К-2); наружные стены 400 мм, перегородки 120 мм приняты (К-1); разрешённая мощность 15 кВт принята по типовым ТУ для частного дома (К-4); подрайон климата не задан — принят не северный (жилые от 2,5 м) (К-7).

См. лист открытых вопросов (лист 7, записи К-1, К-2, К-4, К-7).

Примечания

1. Размеры — в мм. Отступы ковров — от чистовых стен; высоты картин и зеркал — от чистого пола до центра или низа рамы.
2. Шторы — на шинах в нишах потолка (ниша — план потолков, лист 55); закладная под шину — до обшивки ГКЛ. Схемы окон, длины полотен и сборка — лист 80.
3. Картины и зеркала массой более 5 кг — на анкеры по основанию, нагрузка крепежа не меньше двойной массы изделия; на ГКЛ — только по закладной. Декор не перекрывает розетки и выключатели.
4. Ковры на гладком полу — на противоскользящей подложке.
5. Мебель — по плану расстановки мебели (лист 24); ведомость текстиля — лист 81, ведомость декора и схемы развески — лист 83.
6. Номера помещений — по экспликации (лист 15); наименования и площади на этом листе не дублируются.
7. Марки текстиля «Т» и декора «Д» относятся только к листам текстиля и декора; индексы трубопроводов Т1–Т4 — на листах ВК и ОВ.

1000 мм · печать 1:1

Изм.	Кол.уч	Лист	№ док.	Подп.	Дата
Разраб.		Кырлан А.С.			21.10.26
Пров.					
ГИП					
Н. контр.					
Утв.					

ГД-2026-010-АИ

Дом 331 м²

Общая площадь 270,67* м² · * размеры приняты, не замерены (реестр — л. 7, К-1)

Дизайн-проект интерьера

Стадия	Лист	Листов
РП	78	159

План текстиля и декора · 1-й этаж

М 1:100

Кырлан Александр Сергеевич

выпуск 18.10.2026 № 9365d64cec · стр. 82 из 197

План текстиля и декора · Мансарда

Шторы и карнизы, ковры, картины и зеркала, растения · размеры в мм от чистовых стен и чистого пола · марки — по ведомостям

ПРЕДВАРИТЕЛЬНО · не для производства работ · открыто пунктов: 6 (реестр — л. 7)

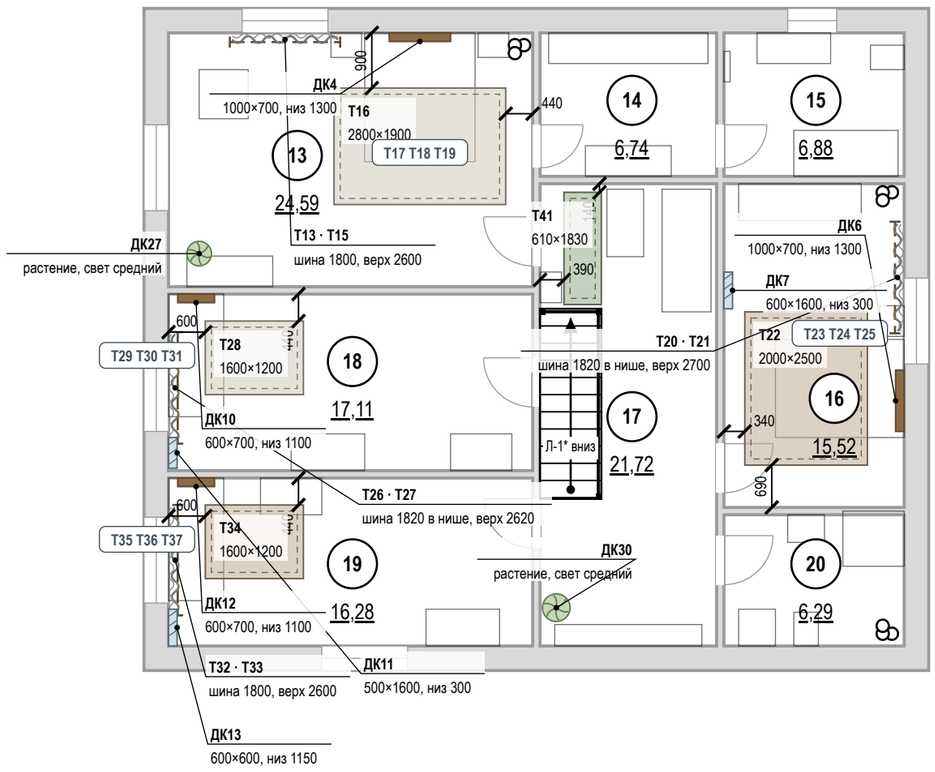

Условные обозначения

- ковёр — габарит в масштабе, цвет изделия
- шина или карниз штор (выше плоскости разреза)
- портьеры (штора-волна)
- тюль (на плане — волнистая линия)
- римская или рулонная штора в проёме
- картина на стене — ширина в масштабе
- зеркало на стене — ширина в масштабе
- растение в кашпо — диаметр в масштабе
- ваза, настольный декор
- подушки, пледы — марки на мебели
- привязка от чистовой стены, мм
- (1) номер помещения, площадь м²
- стены (подложка обмера)

Т1, ДК1 — марки по ведомостям текстиля и декора

Экспликация помещений

лист 15 · на плане — номера в марках

Окна: шина → полотно, мм

Поз.	Шина	Верх шины	Полотно, низ
Т13, Т15	1800	2600	2590, низ 10
Т20, Т21	1820	2700, ниша	2690, низ 10
Т26, Т27	1820	2620, ниша	2610, низ 10
Т32, Т33	1800	2600	2590, низ 10

Развеска: высоты от пола, мм

Поз.	Пом.	Ш×В	Центр	Низ	Стена
ДК4	13	1000×700	1650	1300	А
ДК6	16	1000×700	1650	1300	Б
ДК7	16	600×1600	1100	300	Г
ДК10	18	600×700	1450	1100	А
ДК11	18	500×1600	1100	300	Г
ДК12	19	600×700	1450	1100	А
ДК13	19	600×600	1450	1150	Г

Допущения и предложения на листе

Основа листа: размеры и контуры этажей подобраны проектировщиком по составу помещений и площадям этажей с картинки 470 px (размеры на ней не читаются); обмер и исходный проект — задание (К-1); высоты: 1-й этаж 2800 мм, мансарда 2700 мм (горизонтальная часть) приняты; скаты кровли мансарды приняты по картинке: колено 1200 мм, уклон 45°, конёк вдоль длинной стороны; проект КР — задание (К-2); наружные стены 400 мм, перегородки 120 мм приняты (К-1); разрешённая мощность 15 кВт принята по типовым ТУ для частного дома (К-4); подрайон климата не задан — принят не северный (жилые от 2,5 м) (К-7).

Знак «*» — принято, не замерено и не подтверждено (замерить на объекте): К-6: Л-1 — габарит марша снят с картинки заказчика (11 проступей в холле 3,6 м), а до отм. +3,150 нужно 18 подъёмов — одномаршевая не встаёт: решение по К-6.

См. лист открытых вопросов (лист 7, записи К-1, К-2, К-4, К-6, К-7).

Примечания

1. Размеры — в мм. Отступы ковров — от чистовых стен; высоты картин и зеркал — от чистого пола до центра или низа рамы.
2. Шторы — на шинах в нишах потолка (ниша — план потолков, лист 55); закладная под шину — до обшивки ГКЛ. Схемы окон, длины полотен и сборка — лист 80.
3. Картины и зеркала массой более 5 кг — на анкеры по основанию, нагрузка крепежа не меньше двойной массы изделия; на ГКЛ — только по закладной. Декор не перекрывает розетки и выключатели.
4. Ковры на гладком полу — на противоскользящей подложке.
5. Мебель — по плану расстановки мебели (лист 24); ведомость текстиля — лист 81, ведомость декора и схемы развески — лист 83.
6. Номера помещений — по экспликации (лист 15); наименования и площади на этом листе не дублируются.
7. Марки текстиля «Т» и декора «Д» относятся только к листам текстиля и декора; индексы трубопроводов Т1–Т4 — на листах ВК и ОВ.

1000 мм · печать 1:1

Изм.	Кол.уч	Лист	№ док.	Подп.	Дата
Разраб.		Кырлан А.С.			21.10.26
Пров.					
ГИП					
Н. контр.					
Утв.					

ГД-2026-010-АИ

Дом 331 м²

Общая площадь 270,67* м² · * размеры приняты, не замерены (реестр — л. 7, К-1)

Дизайн-проект интерьера

Стадия	Лист	Листов
РП	79	159

План текстиля и декора · Мансарда

М 1:100

Кырлан Александр Сергеевич

выпуск 18.10.2026 № 9365d64cec · стр. 83 из 197

03

Декор и текстиль

Кырлан Александр Сергеевич

выпуск 18.10.2026 № 9365d64cec · стр. 84 из 197

Шторы и карнизы

Схемы окон «шина → полотно» (М 1:100) · отметки от чистого пола помещения · размеры в мм

Окно 1 — Кухня-столовая (пом. 1): Т14 (М 1:100)

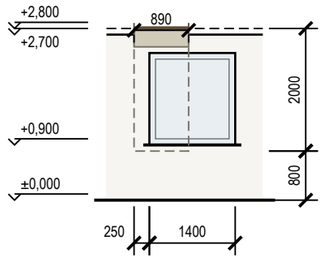

Окно 1 — Кабинет-гостевая (пом. 2): Т7, Т8 (М 1:100)

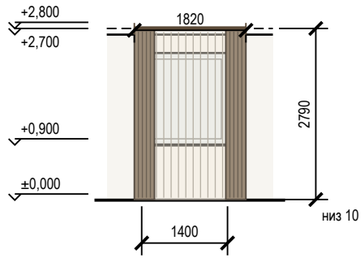

Окно 1 — Гостиная (пом. 5): Т1, Т2 (М 1:100)

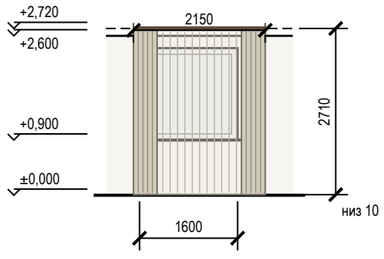

Окно 1 — Спальня мастер (пом. 13): Т13, Т15 (М 1:100)

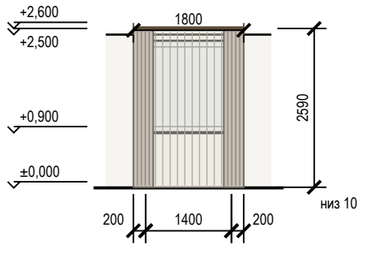

Окно 1 — Спальня 2 (пом. 16): Т20, Т21 (М 1:100)

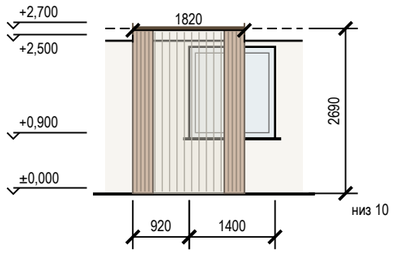

Окно 1 — Спальня 3 (пом. 18): Т26, Т27 (М 1:100)

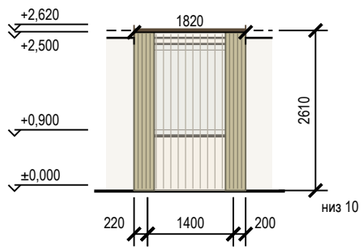

Окно 1 — Спальня 4 (пом. 19): Т32, Т33 (М 1:100)

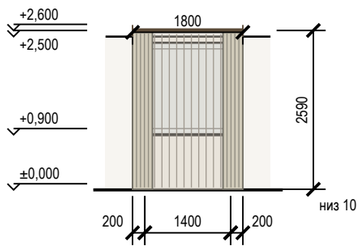

Условные обозначения

- портьеры в открытом положении
- римская штора: сложена / опущена
- верх ниши под шторы в потолке
- тюль (на виде окна — прозрачная плашка)
- шина или карниз на отметке верха
- оконный проём

Допущения и предложения на листе

Основа листа: размеры и контуры этажей подобраны проектировщиком по составу помещений и площадям этажей с картинки 470 px (размеры на ней не читаются); обмер и исходный проект — задание (К-1); высоты: 1-й этаж 2800 мм, мансарда 2700 мм (горизонтальная часть) приняты; скаты кровли мансарды приняты по картинке: колено 1200 мм, уклон 45°, конёк вдоль длинной стороны; проект КР — задание (К-2); наружные стены 400 мм, перегородки 120 мм приняты (К-1); разрешённая мощность 15 кВт принята по типовым ТУ для частного дома (К-4); подрайон климата не задан — принят не северный (жилые от 2,5 м) (К-7).
См. лист открытых вопросов (лист 7, записи К-1, К-2, К-4, К-7).

Примечания

1. Отметки — от чистого пола помещения; размеры — мм. Длины полотен уточняются замером после чистовой отделки пола и потолка, до раскроя.
2. Шины в нишах потолка: закладная (брус или профиль) по всей длине ниши — до обшивки ГКЛ; ниша и её отметка — узел ниши на плане потолков (лист 55).
3. Шина в нише — на отметке верха ниши (крепление к закладной в потолке ниши); длина полотна — от верха шины до чистого пола за вычетом зазора.
4. Полотно портьер «парит» над полом на 10 мм; сборка портьер — 2,0, тюля — 2,5 (ширина полотна — в ведомости текстиля).
5. Шнур римской шторы — с натяжителем, петля низом не ниже 1500 мм от пола (защита детей; EN 13120 — рекомендация).
6. Электрокарнизы не предусмотрены; при замене на электропривод — вывод кабеля в нише у края шины (задание электрику).
7. Марки изделий — по плану текстиля и декора (лист 78) и ведомости текстиля (лист 81).

Изм.	Кол.уч	Лист	№ док.	Подп.	Дата
Разраб.		Кырлан А.С.			21.10.26
Пров.					
ГИП					
Н. контр.					
Утв.					

ГД-2026-010-АИ

Дом 331 м²

Общая площадь 270,67* м² · * размеры приняты, не замерены (реестр — л. 7, К-1)

Дизайн-проект интерьера

Стадия	Лист	Листов
РП	80	159

Шторы и карнизы

М б/м

Кырлан Александр Сергеевич

выпуск 18.10.2026 № 9365d64cec · стр. 85 из 197

Ведомость текстиля

Шторы, тюль, римские шторы, ковры, подушки и пледы · размеры в мм · марки — по плану текстиля и декора

Текстиль: шторы, ковры, подушки, пледы

Поз.	Пом.	Изделие	Размер, мм	Ткань, состав, плотность	Сборка, ширина полотна		Цвет (система, код)	Кол.	Примечание
T1	5	Портьеры-волна, два полотна	шина 2150 × полотно 2710	лён 100 %; 280 г/м²	× 2, ширина 4300		NCS S 2005-Y20R (Светлый песочно-серый)	2	низ 10 (парит); в нише потолка; уход: химчистка; отпаривание на карнизе
T2	5	Тюль-вуаль, одно полотно	шина 2150 × полотно 2710	вуаль; полиэстер 100 %; 60 г/м²	× 2,5, ширина 5375		NCS S 0804-Y30R (тёплый молочный белый)	1	низ 10 (парит); в нише потолка; уход: стирка 30 °C, вешать влажной
T3	5	Ковёр мягкой группы, шерсть с джутом	3600×2400	шерсть с джутом, рельефное плетение; шерсть 100 %			Farrow & Ball No. 243 (Charleston Gray серо-коричневый «камень»)	1	противоскользящая подложка; ворс 12 мм; уход: сухая чистка, пылесос без турбощётки
T4	5	Подушки декоративные на диван, лён	500×500	лён 100 %			Farrow & Ball No. 226 (Joa's White)	3	на Гс2; уход: съёмный чехол, стирка 30 °C
T5	5	Подушки декоративные на диван, акцент	400×600	хлопковый бархат 100 %			Farrow & Ball No. 93 (Studio Green — почти чёрный зелёный)	2	на Гс2; уход: химчистка
T6	5	Плед на диван	1300×1700	шерсть мериноса 100 %			Farrow & Ball No. 93 (Studio Green — почти чёрный зелёный)	1	на Гс2; уход: ручная стирка 30 °C
T7	2	Портьеры на люверсах, шерстяной твид	шина 1820 × полотно 2790	шерстяной твид с подкладкой; лён 100 %; 320 г/м²; блэкаут	× 2, ширина 3640		Farrow & Ball No. 40 (Mouse's Back — тёплый коричнево-серый)	2	низ 10 (парит); в нише потолка
T8	2	Тюль, льняная сетка	шина 1820 × полотно 2790	лён-сетка; полиэстер 100 %	× 2,5, ширина 4550		NCS S 0804-Y30R (тёплый молочный белый)	1	низ 10 (парит); в нише потолка
T9	2	Ковёр джутовый под диваном	1700×2300	джут плетёный; шерсть 100 %			Tikkurila X463 (бежевый песчаник)	1	противоскользящая подложка; ворс 6 мм
T10	2	Подушки на диван, кожа	500×500	кожа натуральная, коньяк; букле (шерсть 60 %, полиэстер 40 %)			NCS S 3010-Y30R (орех/лён тёмный)	3	на К63
T11	2	Подушки на кровать, акцент	400×600	хлопковый бархат 100 %			Farrow & Ball No. 298 (Bancha)	2	на К63
T12	2	Плед на кровать	1300×1700	шерсть мериноса 100 %			Farrow & Ball No. 298 (Bancha)	1	на К63
T13	13	Портьеры-волна, шерсть с блэкаут-подкладкой	шина 1800 × полотно 2590	шерсть плотная с блэкаут-подкладкой; лён 100 %; 320 г/м²	× 2, ширина 5000		Farrow & Ball No. 229 (Elephant's Breath тёплый средне-серый с лиловым подтоном)	2	низ 10 (парит); на потолок
T14	1	Рулонная штора кассетная, ткань димаут	шина 890 × полотно 2000	ткань димаут с грязеотталкивающей пропиткой; полиэстер 100 %			NCS S 2005-Y20R (Светлый песочно-серый)	1	низ 800; в нише потолка; шнур: петля —, cordless; уход: протирка влажной губкой
T15	13	Тюль	шина 1800 × полотно 2590	вуаль; полиэстер 100 %	× 2,5, ширина 6250		Little Greene No. 105 (Slaked Lime)	1	низ 10 (парит); на потолок
T16	13	Ковёр под кроватью, шерсть ручного ткачества	2800×1900	шерсть, ручное ткачество; шерсть 80 %, хлопок 20 %			NCS S 2005-Y20R (Светлый песочно-серый)	1	противоскользящая подложка; ворс 10 мм
T17	13	Подушки декоративные на кровать, шерсть-меланж	500×500	шерсть-меланж; лён 100 %			NCS S 2005-Y20R (Светлый песочно-серый)	3	на М1
T18	13	Подушки на кровать, акцент	400×600	хлопковый бархат 100 %			NCS S 7020-G10Y (Хвойный тёмно-зелёный)	2	на М1
T19	13	Плед на кровать	1300×1700	шерсть мериноса 100 %			NCS S 7020-G10Y (Хвойный тёмно-зелёный)	1	на М1
T20	16	Портьеры-волна, хлопок-сатин с блэкаут-подкладкой	шина 1820 × полотно 2690	хлопок-сатин с блэкаут-подкладкой; лён 100 %; 320 г/м²	× 2, ширина 3640		Tikkurila X463 (бежевый песчаник)	2	низ 10 (парит); в нише потолка
T21	16	Тюль, лён-вуаль	шина 1820 × полотно 2690	лён-вуаль; полиэстер 100 %	× 2,5, ширина 4550		Little Greene No. 105 (Slaked Lime)	1	низ 10 (парит); в нише потолка
T22	16	Ковёр под кроватью, шерсть с узором ромбы	2000×2500	шерсть, ворсовый, узор ромбы; шерсть 100 %			NCS S 3010-Y30R (орех/лён тёмный)	1	противоскользящая подложка; ворс 15 мм
T23	16	Подушки декоративные на кровать, хлопок-рогожка	500×500	хлопок-рогожка; букле (шерсть 60 %, полиэстер 40 %)			Tikkurila X463 (бежевый песчаник)	3	на С1
T24	16	Подушки на кровать, акцент	400×600	хлопковый бархат 100 %			Farrow & Ball No. 64 (Red Earth)	2	на С1
T25	16	Плед на кровать	1300×1700	шерсть мериноса 100 %			Farrow & Ball No. 64 (Red Earth)	1	на С1

Продолжение ведомости — на следующем листе; итог и примечания — на последнем листе ведомости.

Допущения и предложения на листе

Основа листа: размеры и контуры этажей подобраны проектировщиком по составу помещений и площадям этажей с картинки 470 px (размеры на ней не читаются); обмер и исходный проект — задание (К-1); высоты: 1-й этаж 2800 мм, мансарда 2700 мм (горизонтальная часть) приняты; скаты кровли мансарды приняты по картинке: колено 1200 мм, уклон 45°, конёк вдоль длинной стороны; проект КР — задание (К-2); наружные стены 400 мм, перегородки 120 мм приняты (К-1); разрешённая мощность 15 кВт принята по типовым ТУ для частного дома (К-4); подрайон климата не задан — принят не северный (жилые от 2,5 м) (К-7).

См. лист открытых вопросов (лист 7, записи К-1, К-2, К-4, К-7).

Изм.	Кол.уч	Лист	№ док.	Подп.	Дата
Разраб.		Кырлан А.С.			21.10.26
Пров.					
ГИП					
Н. контр.					
Утв.					

ГД-2026-010-АИ

Дом 331 м²

Общая площадь 270,67* м² · * размеры приняты, не замерены (реестр — л. 7, К-1)

Дизайн-проект интерьера

Стадия	Лист	Листов
РП	81	159

Ведомость текстиля

М б/м

Кырлан Александр Сергеевич

выпуск 18.10.2026 № 9365d64cec · стр. 86 из 197

Ведомость текстиля (продолжение)

Шторы, тюль, римские шторы, ковры, подушки и пледы · размеры в мм · марки — по плану текстиля и декора

Текстиль: шторы, ковры, подушки, пледы (продолжение)

Поз.	Пом.	Изделие	Размер, мм	Ткань, состав, плотность	Сборка, ширина полотна		Цвет (система, код)	Кол.	Примечание
T26	18	Портьеры на люверсах, хлопок-канвас с блэкаут-подкладкой	шина 1820 × полотно 2610	хлопок-канвас с блэкаут-подкладкой; лён 100 %; 320 г/м²	× 2, ширина 3640		Tikkurila V451 (выцветший оливковый)	2	низ 10 (парит); в нише потолка
T27	18	Тюль, хлопковая кисея	шина 1820 × полотно 2610	хлопковая кисея; полиэстер 100 %	× 2,5, ширина 4550		NCS S 0804-Y30R (тёплый молочный белый)	1	низ 10 (парит); в нише потолка
T28	18	Ковёр под кроватью, хлопок, стираемый	1600×1200	хлопок, плоское плетение, стираемый; шерсть 100 %			NCS S 2005-Y20R (Светлый песочно-серый)	1	противоскользящая подложка; ворс 5 мм
T29	18	Подушки на кровать, хлопок-вельвет	500×500	хлопок-вельвет; букле (шерсть 60 %, полиэстер 40 %)			Tikkurila V451 (выцветший оливковый)	3	на Д1
T30	18	Подушки на кровать, акцент	400×600	хлопковый бархат 100 %			NCS S 3020-G30Y (шалфей)	2	на Д1
T31	18	Плед на кровать	1300×1700	шерсть мериноса 100 %			NCS S 3020-G30Y (шалфей)	1	на Д1
T32	19	Портьеры-волна, лён-меланж с блэкаут-подкладкой	шина 1800 × полотно 2590	лён-меланж с блэкаут-подкладкой; лён 100 %; 320 г/м²	× 2, ширина 3640		NCS S 2005-Y20R (Светлый песочно-серый)	2	низ 10 (парит); на потолок
T33	19	Тюль, лён-вуаль в мелкую клетку	шина 1800 × полотно 2590	лён-вуаль; полиэстер 100 %	× 2,5, ширина 4550		Farrow & Ball No. 226 (Joa's White)	1	низ 10 (парит); на потолок
T34	19	Ковёр под кроватью, шерсть с узором «горы»	1600×1200	шерсть, ворсовый, тафтинг; шерсть 100 %			NCS S 3010-Y30R (орех/лён тёмный)	1	противоскользящая подложка; ворс 12 мм
T35	19	Подушки на кровать, хлопок-канвас с принтом	500×500	хлопок-канвас с принтом; букле (шерсть 60 %, полиэстер 40 %)			Tikkurila X463 (бежевый песчаник)	3	на Д4
T36	19	Подушки на кровать, акцент	400×600	хлопковый бархат 100 %			NCS S 3040-Y70R (обожжённая глина)	2	на Д4
T37	19	Плед на кровать	1300×1700	шерсть мериноса 100 %			NCS S 3040-Y70R (обожжённая глина)	1	на Д4
T40	10	Покрытие резиновое модульное 500×500×10 мм под спортзону	1500×6300	резиновая крошка SBR с цветными EPDM-вкраплениями, плиты 500×500, 10 мм			Farrow & Ball No. 243 (Charleston Gray серо-коричневый «камень»)	1	
T41	17	Коврик для йоги и растяжки 1830×610×6, TPE, нескользящий	610×1830	TPE, 6 мм, двухслойный			NCS S 3020-G30Y (шалфей)	1	

образец цвета — по HEX производителя краски, справочно

Итого: шторы и тюль — 19 шт.; ковры и дорожки — 8 шт.; подушки, пледы, покрывала — 36 шт.

Образцы по помещениям

1. Кухня-столовая

T14

2. Кабинет-гостевая

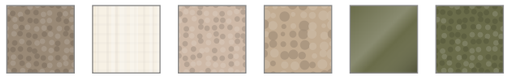

T7 T8 T9 T10 T11 T12

5. Гостиная

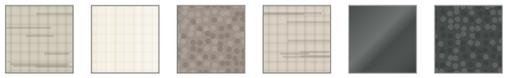

T1 T2 T3 T4 T5 T6

10. Гараж

T40

13. Спальня мастер

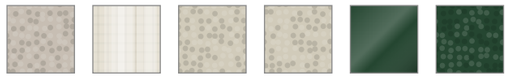

T13 T15 T16 T17 T18 T19

Примечания

1. Коды цвета — ориентир подбора по веерам производителей красок; ткань утверждается по образцу при дневном свете и при свете проекта 2700–3000 K.
2. Размеры полотен — по замеру после чистовой отделки пола и потолка; ширина полотна указана с учётом сборки, без припусков на швы. Схемы окон и отметки шин лист 80.
3. Портьеры и тюль — на тесьме «волна» по системе шины; блэкаут — подкладкой. Ковры — на противоскользящей подложке.
4. Замена изделия — аналогом по характеристикам (состав, плотность, размер, цвет по образцу) с согласованием автора проекта.
5. Места изделий — план текстиля и декора (лист 78); подушки и пледы — по марке мебели.

Допущения и предложения на листе

Основа листа: размеры и контуры этажей подобраны проектировщиком по составу помещений и площадям этажей с картинки 470 px (размеры на ней не читаются); обмер и исходный проект — задание (К-1); высоты: 1-й этаж 2800 мм, мансарда 2700 мм (горизонтальная часть) приняты; скаты кровли мансарды приняты по картинке: колено 1200 мм, уклон 45°, конёк вдоль длинной стороны; проект КР — задание (К-2); наружные стены 400 мм, перегородки 120 мм приняты (К-1); разрешённая мощность 15 кВт принята по типовым ТУ для частного дома (К-4); подрайон климата не задан — принят не северный (жилые от 2,5 м) (К-7).

См. лист открытых вопросов (лист 7, записи К-1, К-2, К-4, К-7).

Изм.	Кол.уч	Лист	№ док.	Подп.	Дата
Разраб.		Кырлан А.С.			21.10.26
Пров.					
ГИП					
Н. контр.					
Утв.					

ГД-2026-010-АИ

Дом 331 м²

Общая площадь 270,67* м² · * размеры приняты, не замерены (реестр — л. 7, К-1)

Дизайн-проект интерьера

Стадия	Лист	Листов
РП	82	159

Ведомость текстиля (продолжение)

М б/м

Кырлан Александр Сергеевич

выпуск 18.10.2026 № 9365d64cec · стр. 87 из 197

Ведомость декора. Схемы развески

Картины, зеркала, растения, настольный декор · схемы развески (М 1:50) · высоты — мм от чистого пола

ПРЕДВАРИТЕЛЬНО · не для производства работ · открыто пунктов: 6 (реестр — л. 7)

Декор: картины, зеркала, растения, предметы

картина · зеркало · мебель под изделием

Поз.	Пом.	Предмет	Размер, мм	Место: стена, высота от пола, мм	Масса, кг	Крепёж и основание	Свет места, отделка	Кол.
ДК1	5	Картина над буфетом: Еловый лес в тумане над горным озером, масло	1200×900	стена Б, привязка 2740; низ 1000, центр 1450; над Гс6	6	планка на дюбелях, 4 точки; основание: перегородка 120 мм; нагрузка 20 кг		1
ДК2	5	Фикус лировидный в кашпо Ø400	450×450	напольное			свет яркий рассеянный	1
ДК3	2	Картина над диваном: Старинная карта горного хребта, офорт в паспарту	1000×700	стена Г, привязка 1700; низ 1100, центр 1450; над К63	4	подвес по основанию, 2 точки	рама — дуб	1
ДК4	13	Картина над кроватью: Ветви лиственницы с шишками, акварель	1000×700	стена А, привязка 3600; низ 1300, центр 1650; над М1	4	подвес по основанию, 2 точки	рама — дуб	1
ДК5	8	Зеркало	800×1800	стена Б, привязка 540; низ 550, центр 1450	18	анкер, 4 шт.; основание: перегородка — определить обмером до монтажа; нагрузка 40 кг	рама — чёрный матовый металл	1
ДК6	16	Картина над кроватью: Глиняный кувшин с полевыми цветами, масло	1000×700	стена Б, привязка 3040; низ 1300, центр 1650; над С1	4	подвес по основанию, 2 точки	рама — дуб	1
ДК7	16	Зеркало в рост в раме из ясеня	600×1600	стена Г, привязка 1440; низ 300, центр 1100	12	анкер для пустотелых оснований, 4 шт.; основание: перегородка — определить обмером до монтажа; нагрузка 30 кг	рама — чёрный матовый металл	1
ДК8	1	Часы настенные Ø400	400×400	стена В, привязка 1200; центр 1550	2	дюбель с крюком, 1 точка; основание: перегородка 120 мм; нагрузка 10 кг		1
ДК9	1	Хлорофитум хохлатый на подоконнике (отм. +0,800)	300×200	напольное			свет средний	1
ДК10	18	Картина над кроватью: Рыжая лиса под ёлкой, детская иллюстрация	600×700	стена А, привязка 150; низ 1100, центр 1450; над Д1	4	подвес по основанию, 2 точки	рама — дуб	1
ДК11	18	Зеркало безопасное (плёнка), рама — светлый ясень	500×1600	стена Г, привязка 2340; низ 300, центр 1100	12	анкер для пустотелых оснований, 4 шт.; основание: перегородка — определить обмером до монтажа; нагрузка 30 кг	рама — чёрный матовый металл	1
ДК12	19	Картина над кроватью: Горы из цветных треугольников, детский принт	600×700	стена А, привязка 150; низ 1100, центр 1450; над Д4	4	подвес по основанию, 2 точки	рама — дуб	1
ДК13	19	Зеркало круглое Ø600 в кожаном ремне	600×600	стена Г, привязка 2140; низ 1150, центр 1450	12	анкер для пустотелых оснований, 4 шт.; основание: перегородка — определить обмером до монтажа; нагрузка 30 кг	рама — чёрный матовый металл	1
ДК21	5	Оливковое дерево в кашпо Ø450	450×450	напольное			свет яркий рассеянный	1
ДК22	5	Ваза с живыми цветами на журнальном столе	200×350	на Гс3				1
ДК23	1	Ваза с тюльпанами на обеденном столе	200×350	на Кх8 (обеденный стол)				1
ДК24	11	Гортензия крупнолистная в кадке Ø500	500×500	напольное			свет средний	1
ДК25	11	Самшит в кадке Ø450	450×450	напольное			свет средний	1
ДК26	11	Папоротник нефролепис в ящике 600×250	250×600	напольное			свет средний	1
ДК27	13	Фикус каучуконосный в кашпо Ø400	400×400	напольное			свет средний	1
ДК28	2	Замиокулькас в кашпо Ø350	350×350	напольное			свет слабый	1
ДК30	17	Монстера в кашпо Ø450 с фитолампой	450×450	напольное			свет средний, фитолампа	1
ДК31	10	Зеркало 1200×1500 для контроля техники, безопасное (плёнка), без рамы	1200×1500	стена Б, привязка 4000; низ 600, центр 1350	22	анкер, 4 шт.; основание: наружная стена 400 мм — материал определить обмером до монтажа; нагрузка 50 кг		1

Допущения и предложения на листе

Основа листа: размеры и контуры этажей подобраны проектировщиком по составу помещений и площадям этажей с картинки 470 px (размеры на ней не читаются); обмер и исходный проект — задание (К-1); высоты: 1-й этаж 2800 мм, мансарда 2700 мм (горизонтальная часть) приняты; скаты кровли мансарды приняты по картинке: колено 1200 мм, уклон 45°, конёк вдоль длинной стороны; проект КР — задание (К-2); наружные стены 400 мм, перегородки 120 мм приняты (К-1); разрешённая мощность 15 кВт принята по типовым ТУ для частного дома (К-4); подрайон климата не задан — принят не северный (жилые от 2,5 м) (К-7).

См. лист открытых вопросов (лист 7, записи К-1, К-2, К-4, К-7).

Примечания

1. Высоты — от чистого пола помещения до низа изделия, «ц» — до центра; привязки — от чистовой грани угла стены, мм.
2. Над мебелью низ изделия — на 150–250 мм выше спинки или изголовья; без мебели центр — на 1450–1600 мм от пола.
3. Изделия до 5 кг — на два подвеса по основанию; тяжелее — на анкеры с нагрузкой не меньше двойной массы; на ГКЛ — только по закладной или анкеру для пустотелых оснований.
4. Зеркала в рост — с креплением от опрокидывания; в санузлах — влагостойкие, на клей для зеркал и нейтральный силикон.
5. Места изделий — план текстиля и декора (лист 78). Схемы ДК1, ДК3, ДК4, ДК5, ДК6, ДК7, ДК8, ДК10, ДК11, ДК12, ДК13, ДК31 — по ведомости и плану.

Изм.	Кол.уч	Лист	№ док.	Подп.	Дата
Разраб.		Кырлан А.С.			21.10.26
Пров.					
ГИП					
Н. контр.					
Утв.					

ГД-2026-010-АИ

Дом 331 м²

Общая площадь 270,67* м² · * размеры приняты, не замерены (реестр — л. 7, К-1)

Дизайн-проект интерьера

Стадия	Лист	Листов
РП	83	159

Ведомость декора. Схемы развески

М б/м

Кырлан Александр Сергеевич

Встроенная мебель. Схема расположения · 1-й этаж

встроенная и корпусная мебель на заказ, кухонный гарнитур · размеры в мм · марки — по ведомости изделий

ПРЕДВАРИТЕЛЬНО · не для производства работ · открыто пунктов: 6 (реестр — л. 7)

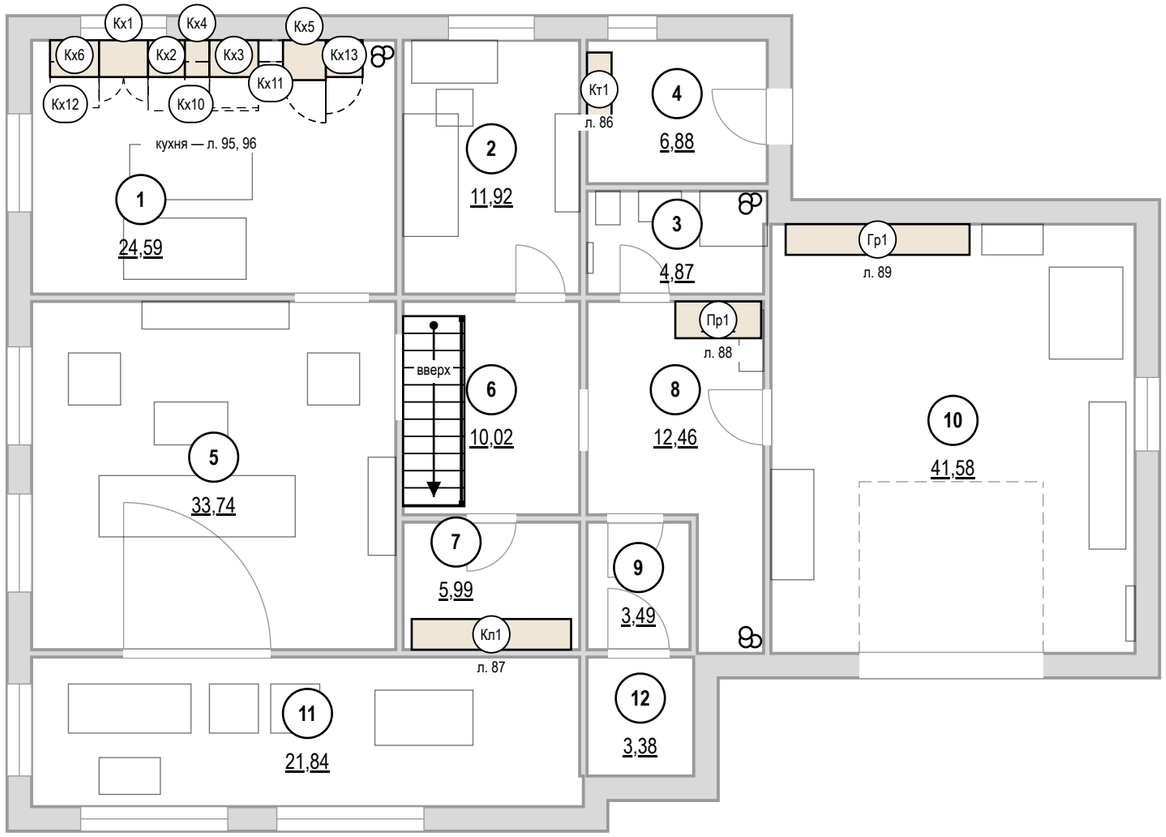

Ведомость изделий

Марка	Наименование	Пом.	Ш×Г×В, мм	Лист
Кт1	Система хранения	4	1200×400×2000	86
Кл1	Система хранения	7	2600×500×2200	87
Пр1	Шкаф-купе	8	1400×600×2600	88
Гр1	Система хранения	10	3000×500×2000	89
Кх6	Модуль нижний: ящики	1	800×600×900	95
Кх12	Модуль навесной: полки	1	500×350×900	95
Кх1	Модуль нижний: мойка	1	800×600×900	95
Кх2	Модуль нижний: ПММ	1	600×600×900	95
Кх10	Модуль навесной: полки	1	600×350×900	95
Кх4	Модуль нижний: ящики	1	400×600×900	95
Кх3	Модуль нижний: духовой шкаф, варочная	1	800×600×900	95
Кх11	Модуль навесной: полки	1	400×350×900	95
Кх5	Пенал: холодильник встр.	1	700×650×2200	95
Кх13	Пенал: полки	1	600×600×2200	95

Условные обозначения

- изделие мебельщика: корпус на полу
- навесной модуль (невидимый контур)
- открывание распашного фасада
- зона выдвижения ящика, двери техники
- дверь купе, стрелка — направление движения
- П5 — марка изделия, под ней — лист изделия

Примечания

1. Изделия — по чистовым размерам помещений; перед раскроем — контрольный замер цеха после чистовой отделки стен, пола и потолка.
2. Открывание фасадов и выдвижение ящиков показано в открытом положении: зоны не пересекают двери, радиаторы, выключатели и проходы.
3. Стояки и счётчики за мебелью — с сервисным люком; газовые трубы мебелью не зашиваются.
4. Покупная мебель — по плану расстановки мебели и спецификации дизайнера; здесь — подложкой.

Допущения и предложения на листе

Основа листа: размеры и контуры этажей подобраны проектировщиком по составу помещений и площадям этажей с картинки 470 px (размеры на ней не читаются); обмер и исходный проект — задание (К-1); высоты: 1-й этаж 2800 мм, мансарда 2700 мм (горизонтальная часть) приняты; скаты кровли мансарды приняты по картинке: колено 1200 мм, уклон 45°, конёк вдоль длинной стороны; проект КР — задание (К-2); наружные стены 400 мм, перегородки 120 мм приняты (К-1); разрешённая мощность 15 кВт принята по типовым ТУ для частного дома (К-4); подрайон климата не задан — принят не северный (жилые от 2,5 м) (К-7).
См. лист открытых вопросов (лист 7, записи К-1, К-2, К-4, К-7).

1000 мм · печать 1:1

Изм.	Кол.уч	Лист	№ док.	Подп.	Дата
Разраб.		Кырлан А.С.			21.10.26
Пров.					
ГИП					
Н. контр.					
Утв.					

ГД-2026-010-АИ

Дом 331 м²

Общая площадь 270,67* м² · * размеры приняты, не замерены (реестр — л. 7, К-1)

Дизайн-проект интерьера	Стадия	Лист	Листов
	РП	84	159

Встроенная мебель. Схема расположения · 1-й этаж

М 1:100

Кырлан Александр Сергеевич

выпуск 18.10.2026 № 9365d64cec · стр. 89 из 197

Встроенная мебель. Схема расположения · Мансарда

встроенная и корпусная мебель на заказ, кухонный гарнитур · размеры в мм · марки — по ведомости изделий

ПРЕДВАРИТЕЛЬНО · не для производства работ · открыто пунктов: 6 (реестр — л. 7)

Ведомость изделий

Марка	Наименование	Пом.	Ш×Г×В, мм	Лист
Гм2	Система хранения	14	1400×500×2400	90
С3	Шкаф распашной	16	2000×600×2400	91
Сп3	Система хранения	17	2400×350×900	92
Д3	Шкаф распашной	18	1000×600×2200	93
Д6	Шкаф распашной	19	1000×600×2200	94

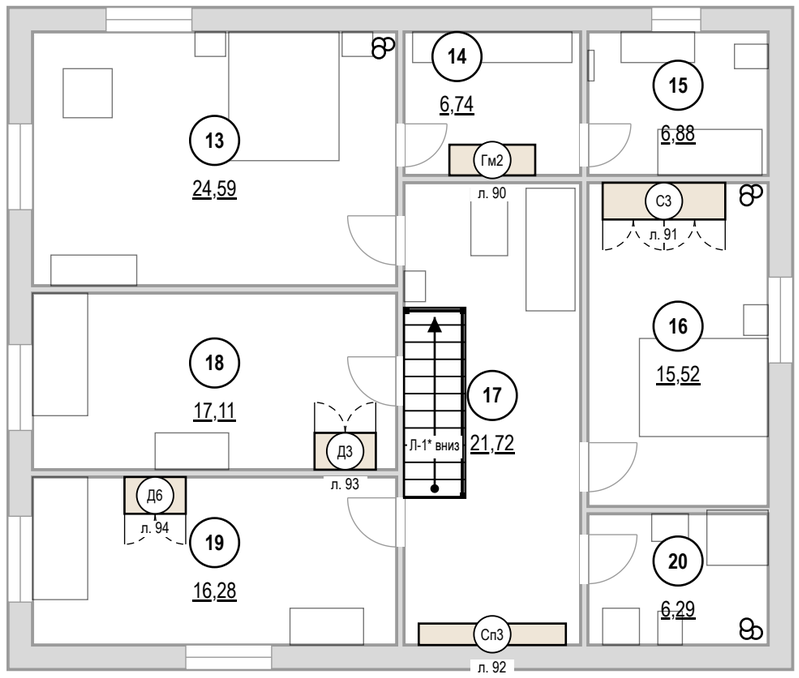

Условные обозначения

- изделие мебельщика: корпус на полу
- навесной модуль (невидимый контур)
- открывание распашного фасада
- зона выдвижения ящика, двери техники
- дверь купе, стрелка — направление движения
- П5 — марка изделия, под ней — лист изделия

Допущения и предложения на листе

Основа листа: размеры и контуры этажей подобраны проектировщиком по составу помещений и площадям этажей с картинки 470 px (размеры на ней не читаются); обмер и исходный проект — задание (К-1); высоты: 1-й этаж 2800 мм, мансарда 2700 мм (горизонтальная часть) приняты; скаты кровли мансарды приняты по картинке: колено 1200 мм, уклон 45°, конёк вдоль длинной стороны; проект КР — задание (К-2); наружные стены 400 мм, перегородки 120 мм приняты (К-1); разрешённая мощность 15 кВт принята по типовым ТУ для частного дома (К-4); подрайон климата не задан — принят не северный (жилые от 2,5 м) (К-7).

Знак «*» — принято, не замерено и не подтверждено (замерить на объекте): К-6: Л-1 — габарит марша снят с картинки заказчика (11 проступей в холле 3,6 м), а до отм. +3,150 нужно 18 подъёмов — одномаршевая не встаёт: решение по К-6.

См. лист открытых вопросов (лист 7, записи К-1, К-2, К-4, К-6, К-7).

Примечания

1. Изделия — по чистовым размерам помещений; перед раскроем — контрольный замер цеха после чистовой отделки стен, пола и потолка.
2. Открывание фасадов и выдвижение ящиков показано в открытом положении: зоны не пересекают двери, радиаторы, выключатели и проходы.
3. Стояки и счётчики за мебелью — с сервисным люком; газовые трубы мебелью не зашиваются.
4. Покупная мебель — по плану расстановки мебели и спецификации дизайнера; здесь — подложкой.

1000 мм · печать 1:1

Изм.	Кол.уч	Лист	№ док.	Подп.	Дата
Разраб.		Кырлан А.С.			21.10.26
Пров.					
ГИП					
Н. контр.					
Утв.					

ГД-2026-010-АИ

Дом 331 м²

Общая площадь 270,67* м² · * размеры приняты, не замерены (реестр — л. 7, К-1)

Дизайн-проект интерьера

Стадия	Лист	Листов
РП	85	159

Встроенная мебель. Схема расположения · Мансарда

М 1:100

Кырлан Александр Сергеевич

выпуск 18.10.2026 № 9365d64cec · стр. 90 из 197

Система хранения Кт1

Котельная (пом. 4) · вид из помещения · размеры в мм, отметки в м

ПРЕДВАРИТЕЛЬНО · не для производства работ · открыто пунктов: 6 (реестр — л. 7)

Общий вид

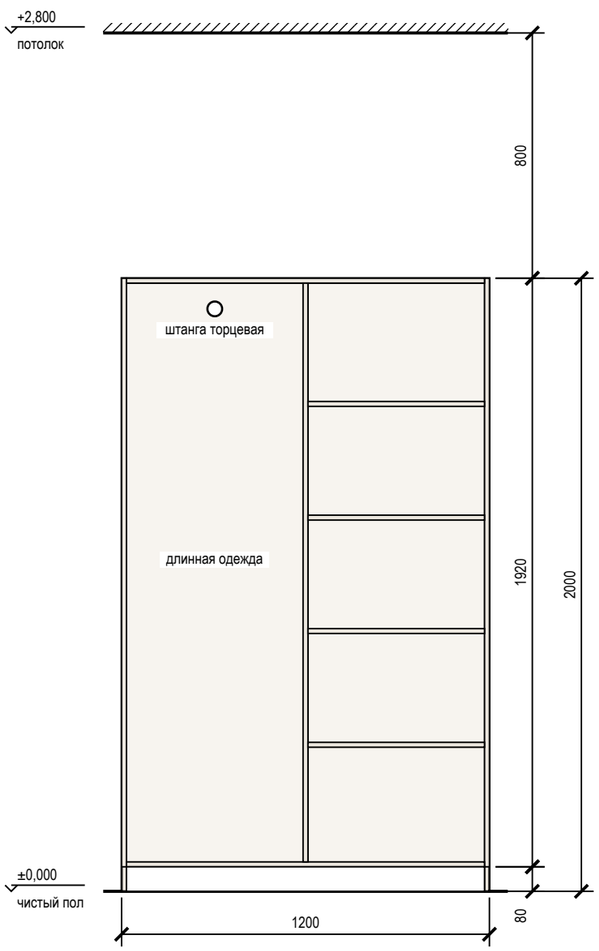

Наполнение, размеры в свету

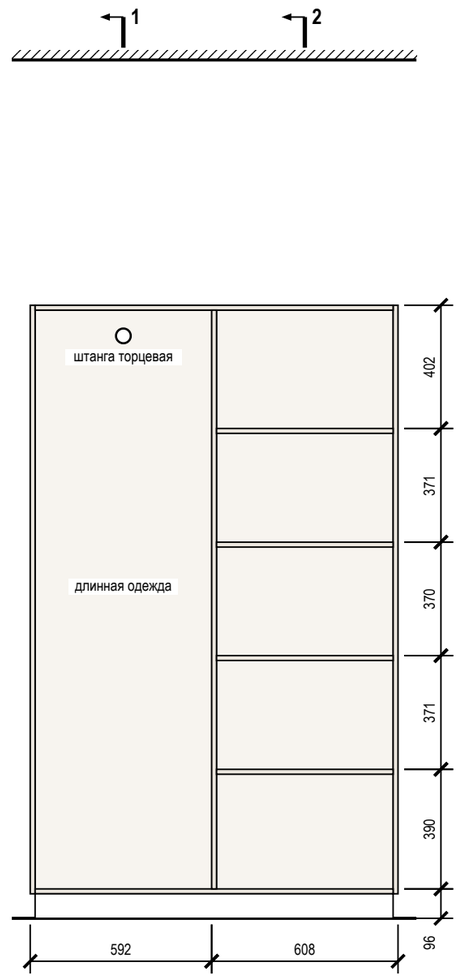

Разрез 1-1

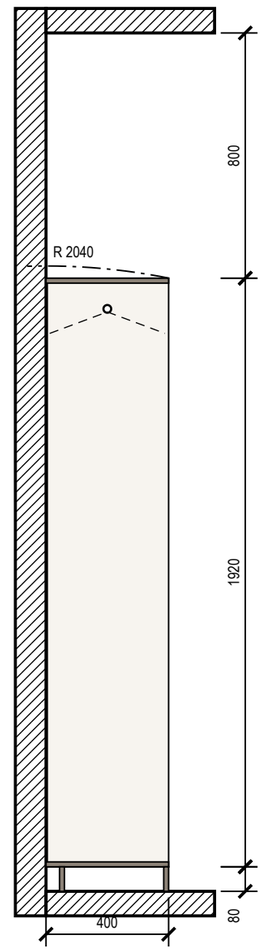

Разрез 2-2

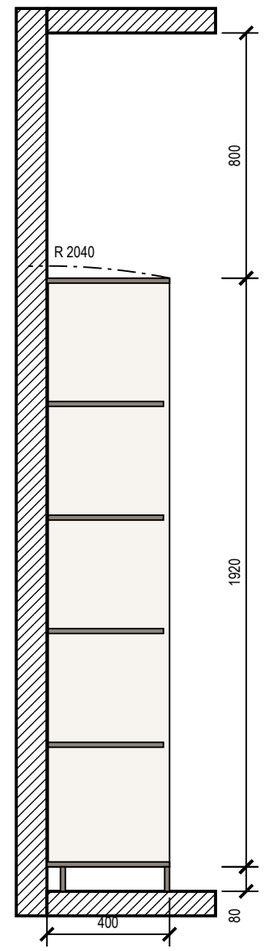

Примечания

1. Размеры — в мм по чистовой отделке; изделие 1200×400×2000 (Ш×Г×В). Перед раскроем — контрольный замер цеха после чистовой отделки стен, пола и потолка.
2. Корпус — ЛДСП 16 мм, задняя стенка ХДФ 4 мм в паз, цоколь 80 мм на регулируемых опорах; открытая система без фасадов, ящики с фасадами.
3. Кромка: скрытые торцы 0,4 мм, видимые 2 мм (ПВХ/АБС).
4. Номинальные зазоры: между фасадами ящиков 3 мм, фасад ящика — стойка 2 мм.
5. Ящики — направляющие полного выдвижения NL 350 (внутренняя глубина 396 мм ≥ NL + 3); присадка по 32-й системе — выполняет цех.
6. Зазор до потолка 800 мм.
7. Подъём корпуса: диагональ боковины $\sqrt{(2000^2 + 400^2)} = 2040$ мм < 2800 мм до потолка — корпус собирается лёжа и поднимается поворотом.
8. Крепление к стене от опрокидывания — уголки 2 шт. к несущему основанию (монтажная схема шкафов).

Условные обозначения

- корпус и полки ЛДСП (вид на стену)
- задняя стенка ХДФ
- деталь в разрезе
- штанга для плечиков (на разрезе — плечики 450 мм)
- траектория угла корпуса при подъёме в проектное положение

Допущения и предложения на листе

Основа листа: размеры и контуры этажей подобраны проектировщиком по составу помещений и площадям этажей с картинки 470 px (размеры на ней не читаются); обмер и исходный проект — задание (К-1); высоты: 1-й этаж 2800 мм, мансарда 2700 мм (горизонтальная часть) приняты; скаты кровли мансарды приняты по картинке: колено 1200 мм, уклон 45°, конёк вдоль длинной стороны; проект КР — задание (К-2); наружные стены 400 мм, перегородки 120 мм приняты (К-1); разрешённая мощность 15 кВт принята по типовым ТУ для частного дома (К-4); подрайон климата не задан — принят не северный (жилые от 2,5 м) (К-7).
См. лист открытых вопросов (лист 7, записи К-1, К-2, К-4, К-7).

1000 мм · печать 1:1

Изм.	Кол.уч	Лист	№ док.	Подп.	Дата
Разраб.		Кырлан А.С.			21.10.26
Пров.					
ГИП					
Н. контр.					
Утв.					

ГД-2026-010-АИ

Дом 331 м²

Общая площадь 270,67* м² · * размеры приняты, не замерены (реестр — л. 7, К-1)

Дизайн-проект интерьера

Стадия	Лист	Листов
РП	86	159

Система хранения Кт1

М 1:20

Кырлан Александр Сергеевич

выпуск 18.10.2026 № 9365d64cec · стр. 91 из 197

Система хранения Кл1

Кладовая (пом. 7) · вид из помещения · размеры в мм, отметки в м

ПРЕДВАРИТЕЛЬНО · не для производства работ · открыто пунктов: 6 (реестр — л. 7)

Общий вид

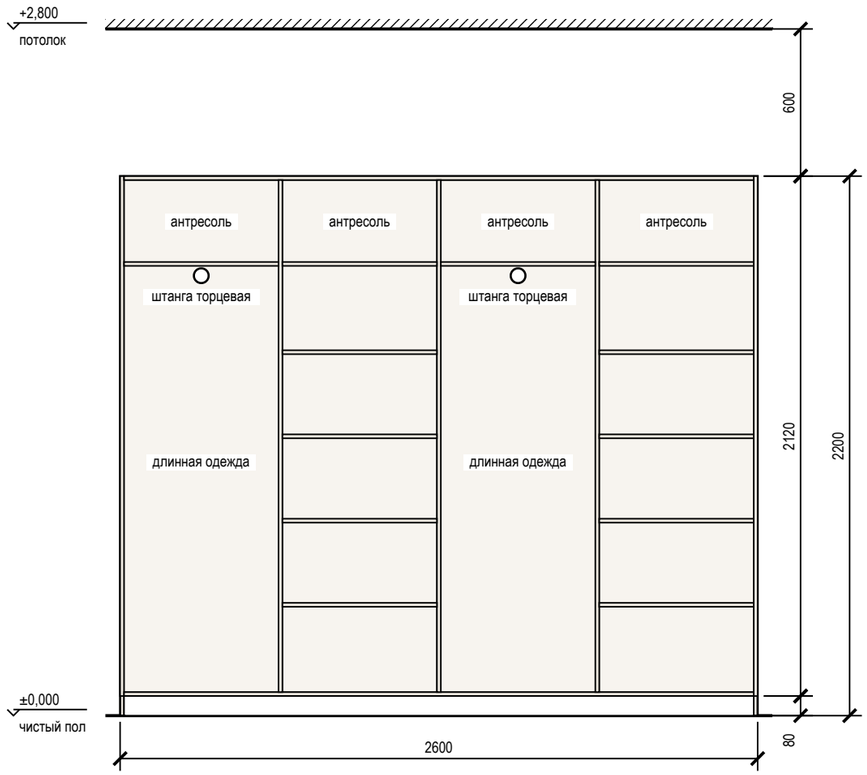

Наполнение, размеры в свету

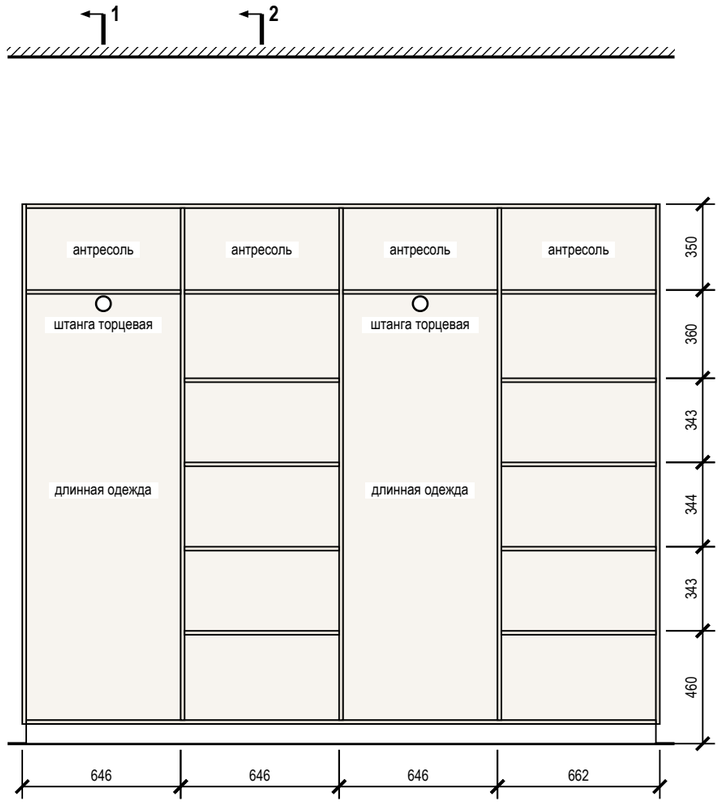

Разрез 1-1

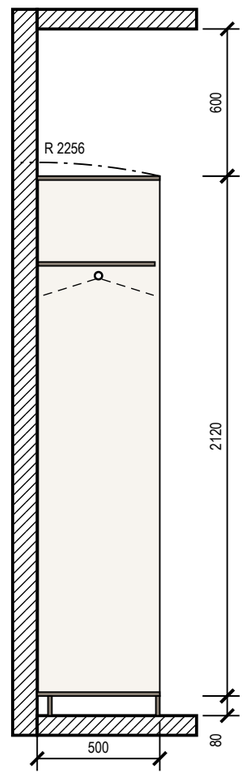

Разрез 2-2

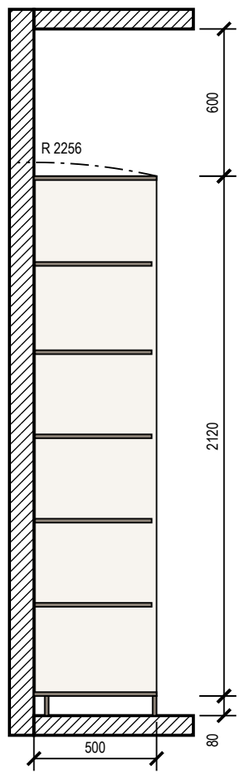

Примечания

1. Размеры — в мм по чистовой отделке; изделие 2600×500×2200 (Ш×Г×В). Перед раскроем — контрольный замер цеха после чистовой отделки стен, пола и потолка.
2. Корпус — ЛДСП 16 мм, задняя стенка ХДФ 4 мм в паз, цоколь 80 мм на регулируемых опорах; открытая система без фасадов, ящики с фасадами.
3. Кромка: скрытые торцы 0,4 мм, видимые 2 мм (ПВХ/АБС).
4. Номинальные зазоры: между фасадами ящиков 3 мм, фасад ящика — стойка 2 мм.
5. Ящики — направляющие полного выдвижения NL 450 (внутренняя глубина 496 мм ≥ NL + 3); присадка по 32-й системе — выполняет цех.
6. Зазор до потолка 600 мм.
7. Подъём корпуса: диагональ боковины $\sqrt{(2200^2 + 500^2)} = 2256$ мм < 2800 мм до потолка — корпус собирается лёжа и поднимается поворотом.
8. Крепление к стене от опрокидывания — уголки 2 шт. к несущему основанию (монтажная схема шкафов).

Условные обозначения

- корпус и полки ЛДСП (вид на стену)
- задняя стенка ХДФ
- деталь в разрезе
- штанга для плечиков (на разрезе — плечики 450 мм)
- траектория угла корпуса при подъёме в проектное положение

Допущения и предложения на листе

Основа листа: размеры и контуры этажей подобраны проектировщиком по составу помещений и площадям этажей с картинки 470 px (размеры на ней не читаются); обмер и исходный проект — задание (К-1); высоты: 1-й этаж 2800 мм, мансарда 2700 мм (горизонтальная часть) приняты; скаты кровли мансарды приняты по картинке: колено 1200 мм, уклон 45°, конёк вдоль длинной стороны; проект КР — задание (К-2); наружные стены 400 мм, перегородки 120 мм приняты (К-1); разрешённая мощность 15 кВт принята по типовым ТУ для частного дома (К-4); подрайон климата не задан — принят не северный (жилые от 2,5 м) (К-7).
См. лист открытых вопросов (лист 7, записи К-1, К-2, К-4, К-7).

1000 мм · печать 1:1

Изм.	Кол.уч	Лист	№ док.	Подп.	Дата
Разраб.		Кырлан А.С.			21.10.26
Пров.					
ГИП					
Н. контр.					
Утв.					

ГД-2026-010-АИ

Дом 331 м²

Общая площадь 270,67* м² · * размеры приняты, не замерены (реестр — л. 7, К-1)

Дизайн-проект интерьера

Стадия	Лист	Листов
РП	87	159

Система хранения Кл1

М 1:25

Кырлан Александр Сергеевич

выпуск 18.10.2026 № 9365d64cec · стр. 92 из 197

Шкаф-купе Пр1

Прихожая (пом. 8) · вид из помещения · размеры в мм, отметки в м

ПРЕДВАРИТЕЛЬНО · не для производства работ · открыто пунктов: 6 (реестр — л. 7)

Вид с фасадами

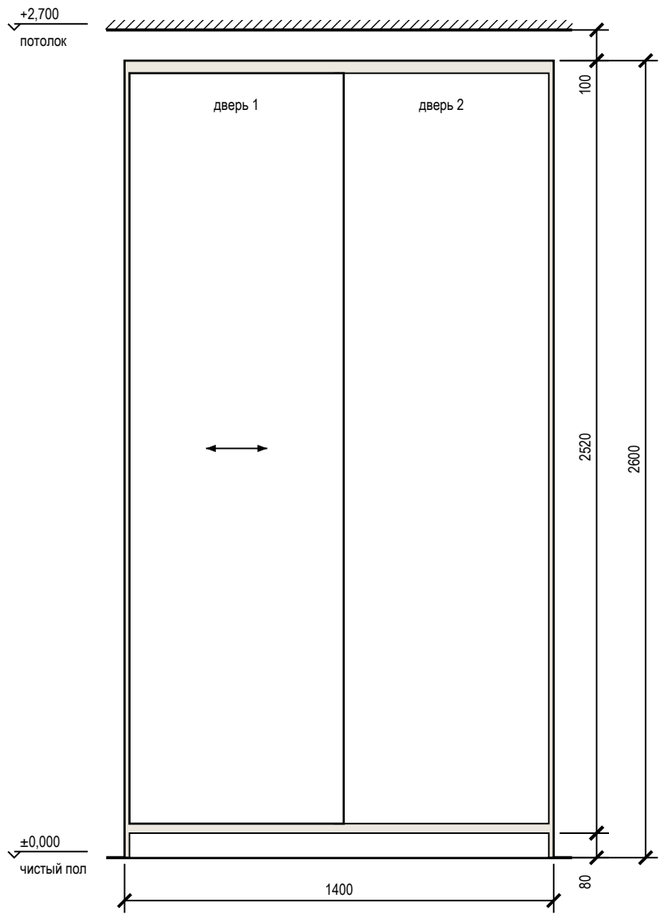

Вид без фасадов

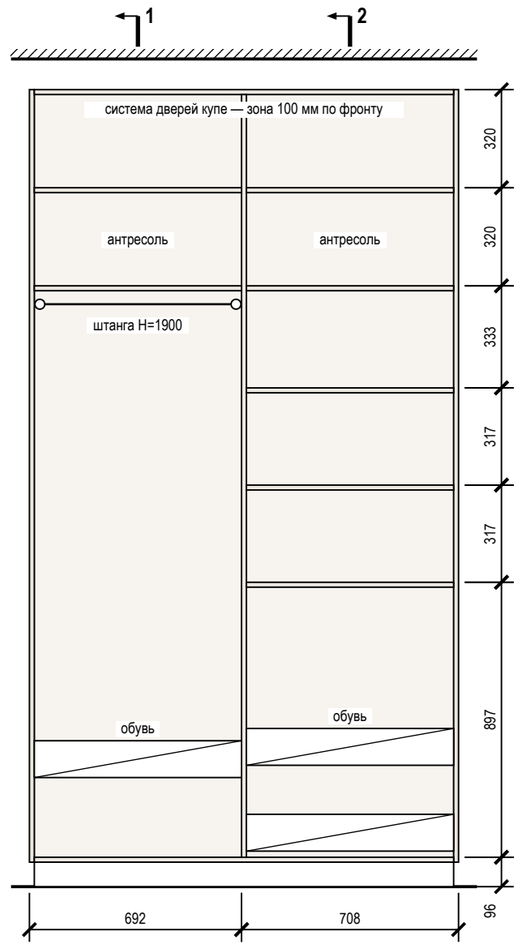

Разрез 1-1

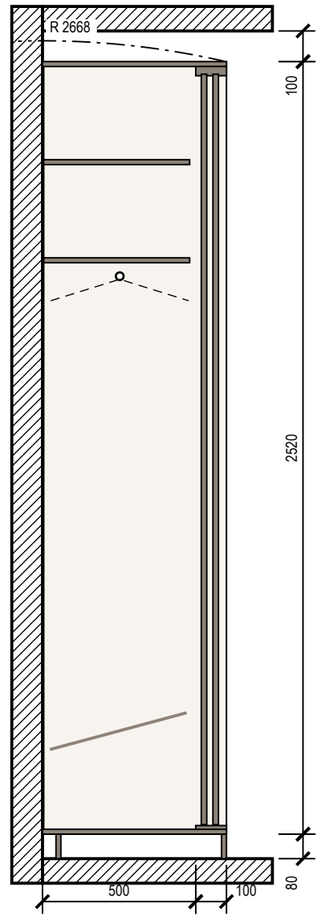

Разрез 2-2

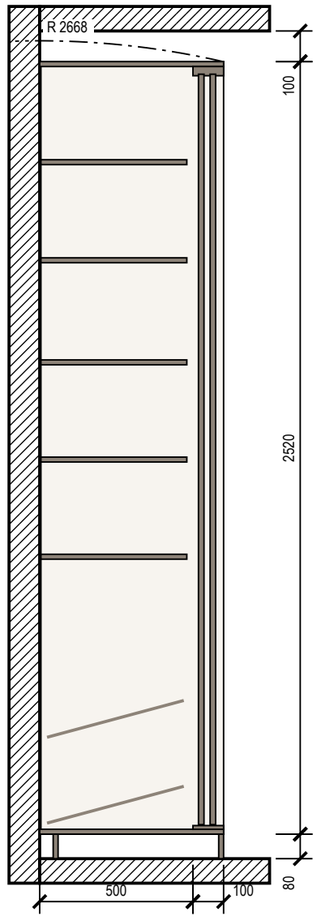

Примечания

1. Размеры — в мм по чистовой отделке; изделие 1400×600×2600 (Ш×Г×В). Перед раскроем — контрольный замер цеха после чистовой отделки стен, пола и потолка.
2. Корпус — ЛДСП 16 мм, задняя стенка ХДФ 4 мм в паз, цоколь 80 мм на регулируемых опорах; двери купе — ЛДСП 10 мм в алюминиевом профиле, нахлёст 30 мм, ширина двери 699 мм, высота — проём минус 40 мм; цвет — по колерной карте.
3. Кромка: скрытые торцы 0,4 мм, видимые 2 мм (ПВХ/АБС).
4. Номинальные зазоры: дверь купе — боковина 3 мм, фасад ящика — стойка 2 мм; ящики внутри купе — с накладкой 30 мм на стойке со стороны нахлёста дверей.
5. Ящики — направляющие полного выдвижения NL 450 (внутренняя глубина 496 мм ≥ NL + 3); присадка по 32-й системе — выполняет цех.
6. Зазор до потолка 100 мм — закрыть планкой в цвет корпуса при монтаже.
7. Подъём корпуса: диагональ боковины $\sqrt{(2600^2 + 600^2)} = 2668$ мм < 2700 мм до потолка — корпус собирается лёжа и поднимается поворотом.
8. Крепление к стене от опрокидывания — уголки 2 шт. к несущему основанию (монтажная схема шкафов).

Условные обозначения

- дверь купе, стрелка — направление движения
- корпус и полки ЛДСП (вид на стену)
- задняя стенка ХДФ
- деталь в разрезе
- штанга для плечиков (на разрезе — плечики 450 мм)
- траектория угла корпуса при подъёме в проектное положение

Допущения и предложения на листе

Основа листа: размеры и контуры этажей подобраны проектировщиком по составу помещений и площадям этажей с картинки 470 px (размеры на ней не читаются); обмер и исходный проект — задание (К-1); высоты: 1-й этаж 2800 мм, мансарда 2700 мм (горизонтальная часть) приняты; скаты кровли мансарды приняты по картинке: колено 1200 мм, уклон 45°, конёк вдоль длинной стороны; проект КР — задание (К-2); наружные стены 400 мм, перегородки 120 мм приняты (К-1); разрешённая мощность 15 кВт принята по типовым ТУ для частного дома (К-4); подрайон климата не задан — принят не северный (жилые от 2,5 м) (К-7).
См. лист открытых вопросов (лист 7, записи К-1, К-2, К-4, К-7).

1000 мм · печать 1:1

Изм.	Кол.уч	Лист	№ док.	Подп.	Дата
Разраб.		Кырлан А.С.			21.10.26
Пров.					
ГИП					
Н. контр.					
Утв.					

ГД-2026-010-АИ

Дом 331 м²

Общая площадь 270,67* м² · * размеры приняты, не замерены (реестр — л. 7, К-1)

Дизайн-проект интерьера

Стадия	Лист	Листов
РП	88	159

Шкаф-купе Пр1

М 1:20

Кырлан Александр Сергеевич

выпуск 18.10.2026 № 9365d64cec · стр. 93 из 197

Система хранения Гр1

Гараж (пом. 10) · вид из помещения · размеры в мм, отметки в м

ПРЕДВАРИТЕЛЬНО · не для производства работ · открыто пунктов: 6 (реестр — л. 7)

Общий вид

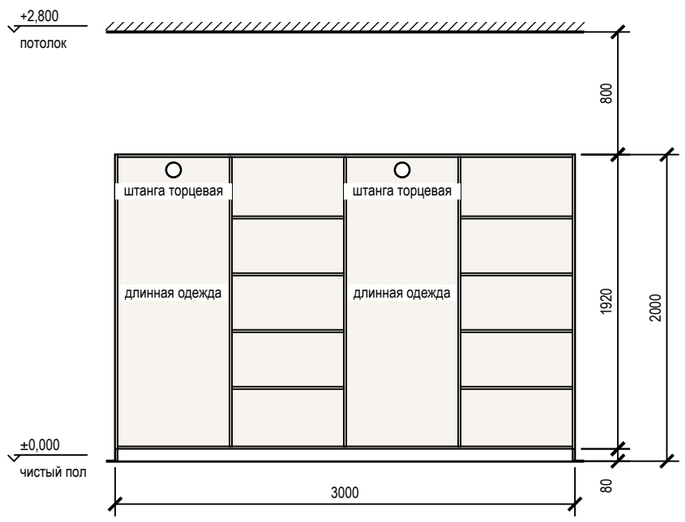

Наполнение, размеры в свету

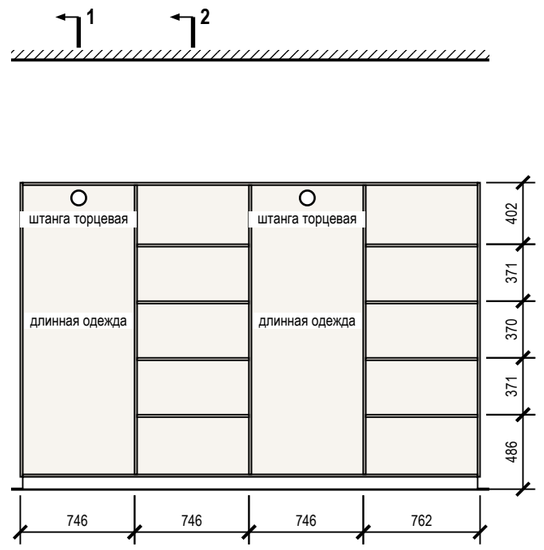

Разрез 1-1

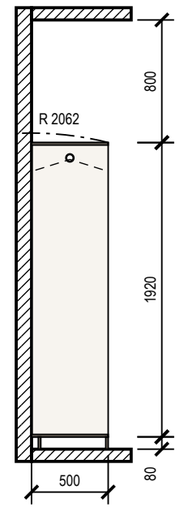

Разрез 2-2

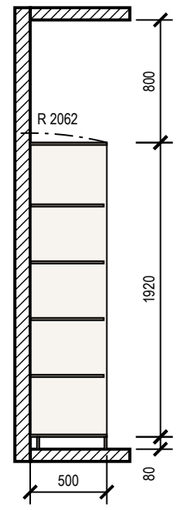

Примечания

1. Размеры — в мм по чистовой отделке; изделие 3000×500×2000 (Ш×Г×В). Перед раскроем — контрольный замер цеха после чистовой отделки стен, пола и потолка.
2. Корпус — ЛДСП 16 мм, задняя стенка ХДФ 4 мм в паз, цоколь 80 мм на регулируемых опорах; открытая система без фасадов, ящики с фасадами.
3. Кромка: скрытые торцы 0,4 мм, видимые 2 мм (ПВХ/АБС).
4. Номинальные зазоры: между фасадами ящиков 3 мм, фасад ящика — стойка 2 мм.
5. Ящики — направляющие полного выдвижения NL 450 (внутренняя глубина 496 мм ≥ NL + 3); присадка по 32-й системе — выполняет цех.
6. Зазор до потолка 800 мм.
7. Подъём корпуса: диагональ боковины √(2000² + 500²) = 2062 мм < 2800 мм до потолка — корпус собирается лёжа и поднимается поворотом.
8. Крепление к стене от опрокидывания: true; основание стены и шаг анкеров — монтажная схема шкафов.

Условные обозначения

- корпус и полки ЛДСП (вид на стену)
- задняя стенка ХДФ
- деталь в разрезе
- штанга для плечиков (на разрезе — плечики 450 мм)
- траектория угла корпуса при подъёме в проектное положение

Допущения и предложения на листе

Основа листа: размеры и контуры этажей подобраны проектировщиком по составу помещений и площадям этажей с картинки 470 px (размеры на ней не читаются); обмер и исходный проект — задание (К-1); высоты: 1-й этаж 2800 мм, мансарда 2700 мм (горизонтальная часть) приняты; скаты кровли мансарды приняты по картинке: колено 1200 мм, уклон 45°, конёк вдоль длинной стороны; проект КР — задание (К-2); наружные стены 400 мм, перегородки 120 мм приняты (К-1); разрешённая мощность 15 кВт принята по типовым ТУ для частного дома (К-4); подрайон климата не задан — принят не северный (жилые от 2,5 м) (К-7).
См. лист открытых вопросов (лист 7, записи К-1, К-2, К-4, К-7).

1000 мм · печать 1:1

Изм.	Кол.уч	Лист	№ док.	Подп.	Дата
Разраб.		Кырлан А.С.			21.10.26
Пров.					
ГИП					
Н. контр.					
Утв.					

ГД-2026-010-АИ

Дом 331 м²

Общая площадь 270,67* м² · * размеры приняты, не замерены (реестр — л. 7, К-1)

Дизайн-проект интерьера

Стадия	Лист	Листов
РП	89	159

Система хранения Гр1

М 1:40

Кырлан Александр Сергеевич

выпуск 18.10.2026 № 9365d64cec · стр. 94 из 197

Система хранения Гм2

Гардеробная мастер (пом. 14) · вид из помещения · размеры в мм, отметки в м

ПРЕДВАРИТЕЛЬНО · не для производства работ · открыто пунктов: 6 (реестр — л. 7)

Общий вид

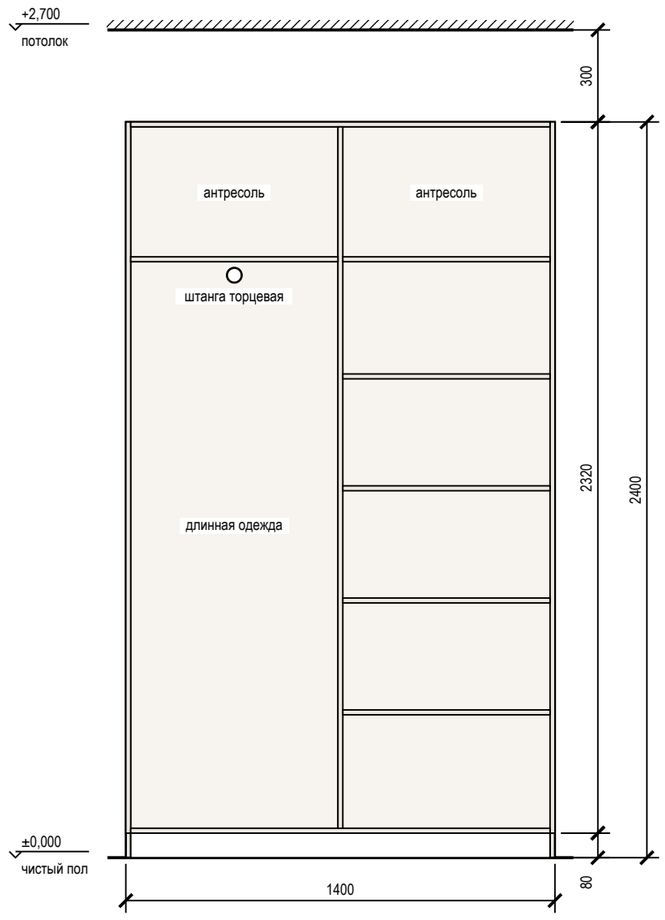

Наполнение, размеры в свету

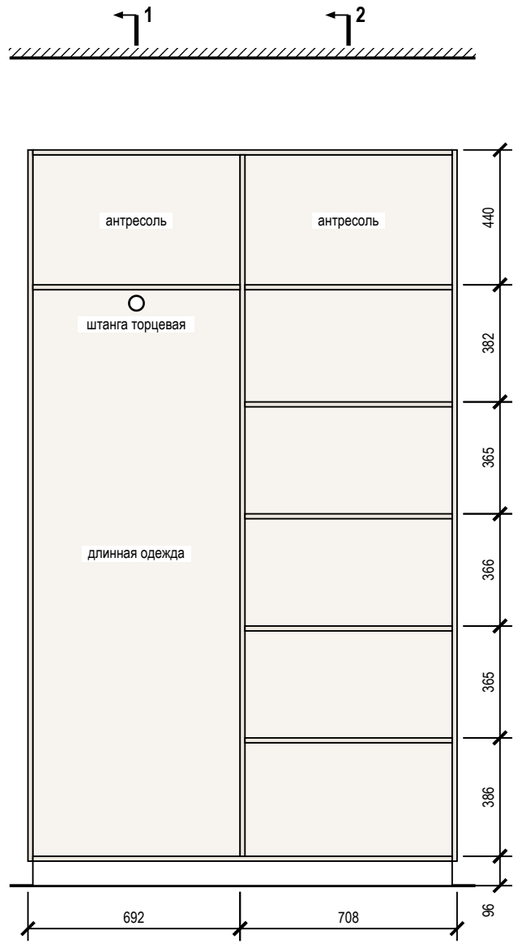

Разрез 1-1

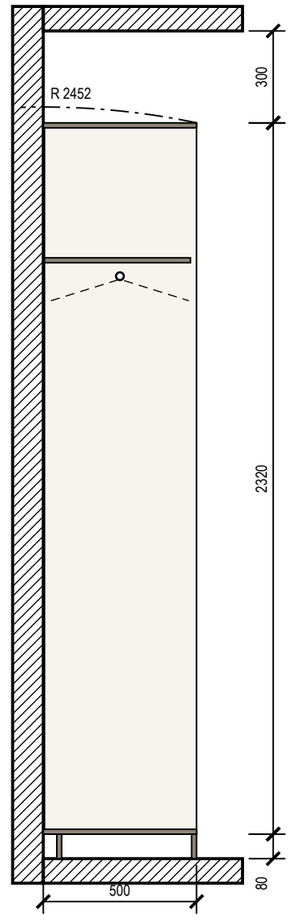

Разрез 2-2

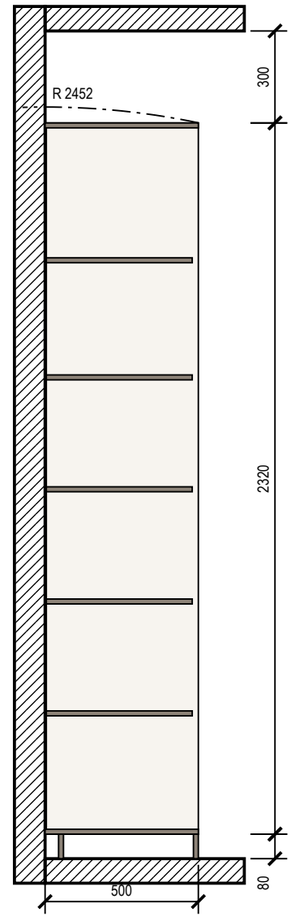

Примечания

1. Размеры — в мм по чистовой отделке; изделие 1400×500×2400 (Ш×Г×В). Перед раскроем — контрольный замер цеха после чистовой отделки стен, пола и потолка.
2. Корпус — ЛДСП 16 мм, задняя стенка ХДФ 4 мм в паз, цоколь 80 мм на регулируемых опорах; открытая система без фасадов, ящики с фасадами.
3. Кромка: скрытые торцы 0,4 мм, видимые 2 мм (ПВХ/АБС).
4. Номинальные зазоры: между фасадами ящиков 3 мм, фасад ящика — стойка 2 мм.
5. Ящики — направляющие полного выдвижения NL 450 (внутренняя глубина 496 мм ≥ NL + 3); присадка по 32-й системе — выполняет цех.
6. Зазор до потолка 300 мм.
7. Подъём корпуса: диагональ боковины $\sqrt{(2400^2 + 500^2)} = 2452$ мм < 2700 мм до потолка — корпус собирается лёжа и поднимается поворотом.
8. Крепление к стене от опрокидывания — уголки 2 шт. к несущему основанию (монтажная схема шкафов).

Условные обозначения

- корпус и полки ЛДСП (вид на стену)
- задняя стенка ХДФ
- деталь в разрезе
- штанга для плечиков (на разрезе — плечики 450 мм)
- траектория угла корпуса при подъёме в проектное положение

Допущения и предложения на листе

Основа листа: размеры и контуры этажей подобраны проектировщиком по составу помещений и площадям этажей с картинки 470 px (размеры на ней не читаются); обмер и исходный проект — задание (К-1); высоты: 1-й этаж 2800 мм, мансарда 2700 мм (горизонтальная часть) приняты; скаты кровли мансарды приняты по картинке: колено 1200 мм, уклон 45°, конёк вдоль длинной стороны; проект КР — задание (К-2); наружные стены 400 мм, перегородки 120 мм приняты (К-1); разрешённая мощность 15 кВт принята по типовым ТУ для частного дома (К-4); подрайон климата не задан — принят не северный (жилые от 2,5 м) (К-7).

См. лист открытых вопросов (лист 7, записи К-1, К-2, К-4, К-7).

1000 мм · печать 1:1

Изм.	Кол.уч	Лист	№ док.	Подп.	Дата
Разраб.		Кырлан А.С.			21.10.26
Пров.					
ГИП					
Н. контр.					
Утв.					

ГД-2026-010-АИ

Дом 331 м²

Общая площадь 270,67* м² · * размеры приняты, не замерены (реестр — л. 7, К-1)

Дизайн-проект интерьера

Стадия	Лист	Листов
РП	90	159

Система хранения Гм2

М 1:20

Кырлан Александр Сергеевич

выпуск 18.10.2026 № 9365d64cec · стр. 95 из 197

Шкаф распашной С3

Спальня 2 (пом. 16) · вид из помещения · размеры в мм, отметки в м

ПРЕДВАРИТЕЛЬНО · не для производства работ · открыто пунктов: 6 (реестр — л. 7)

Вид с фасадами

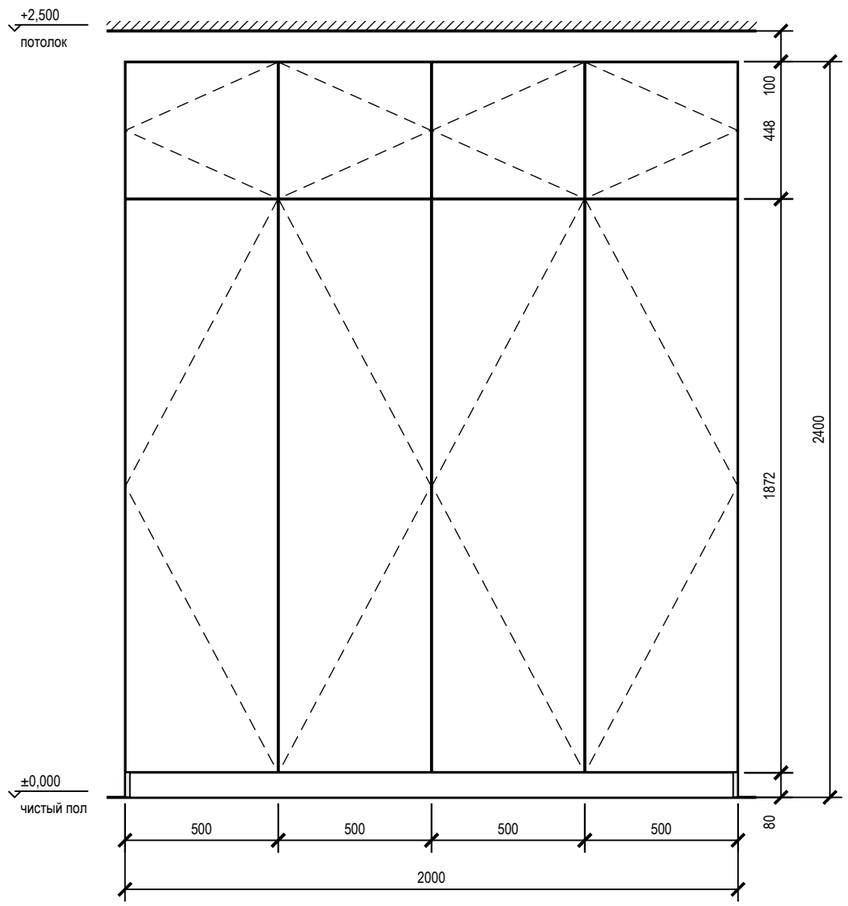

Вид без фасадов

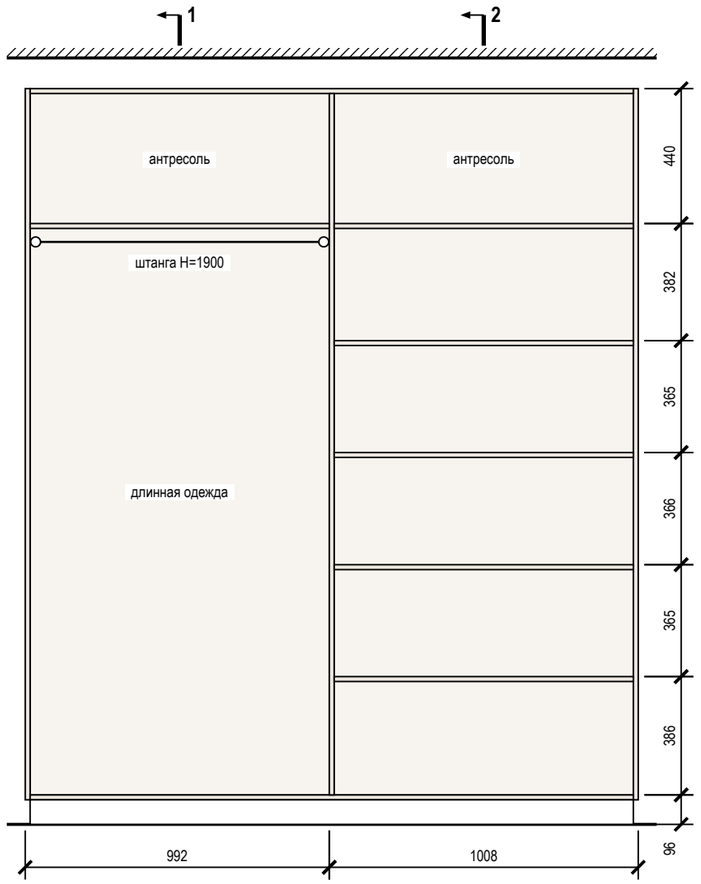

Разрез 1-1

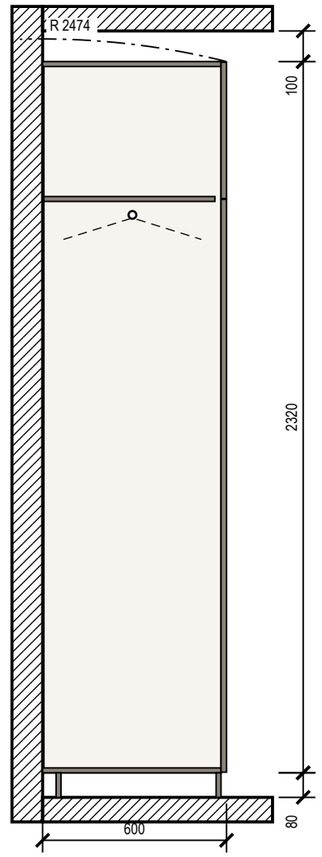

Разрез 2-2

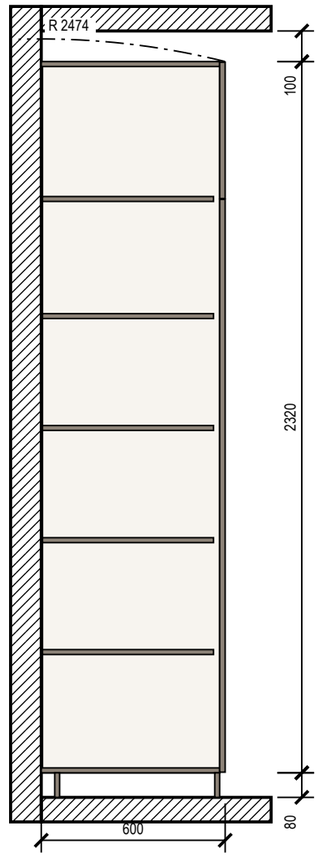

Примечания

1. Размеры — в мм по чистовой отделке; изделие 2000×600×2400 (Ш×Г×В). Перед раскроем — контрольный замер цеха после чистовой отделки стен, пола и потолка.
2. Корпус — ЛДСП 16 мм, задняя стенка ХДФ 4 мм в паз, цоколь 80 мм на регулируемых опорах; фасады — МДФ, эмаль матовая 18 мм накладные, цвет — по колерной карте; петли с доводчиком: фасад 1869 мм — 4 петли, фасад 445 мм — 2 петли.
3. Кромка: скрытые торцы 0,4 мм, видимые 2 мм (ПВХ/АБС).
4. Номинальные зазоры: между фасадами 3 мм, фасад — стена и фасад — потолок не менее 3 мм, фасад ящика — стойка 2 мм.
5. Ящики — направляющие полного выдвижения NL 550 (внутренняя глубина 578 мм ≥ NL + 3); присадка по 32-й системе — выполняет цех.
6. Зазор до потолка 100 мм — закрыть планкой в цвет корпуса при монтаже.
7. Подъём корпуса: диагональ боковины $\sqrt{(2400^2 + 600^2)} = 2474$ мм < 2500 мм до потолка — корпус собирается лёжа и поднимается поворотом.
8. Крепление к стене от опрокидывания — уголки 2 шт. к несущему основанию (монтажная схема шкафов).

Условные обозначения

- фасад распашной: линии сходятся к стороне петель
- корпус и полки ЛДСП (вид на стену)
- задняя стенка ХДФ
- деталь в разрезе
- штанга для плечиков (на разрезе — плечики 450 мм)
- траектория угла корпуса при подъёме в проектное положение

Допущения и предложения на листе

Основа листа: размеры и контуры этажей подобраны проектировщиком по составу помещений и площадям этажей с картинки 470 px (размеры на ней не читаются); обмер и исходный проект — задание (К-1); высоты: 1-й этаж 2800 мм, мансарда 2700 мм (горизонтальная часть) приняты; скаты кровли мансарды приняты по картинке: колено 1200 мм, уклон 45°, конёк вдоль длинной стороны; проект КР — задание (К-2); наружные стены 400 мм, перегородки 120 мм приняты (К-1); разрешённая мощность 15 кВт принята по типовым ТУ для частного дома (К-4); подрайон климата не задан — принят не северный (жилые от 2,5 м) (К-7).
См. лист открытых вопросов (лист 7, записи К-1, К-2, К-4, К-7).

1000 мм · печать 1:1

Изм.	Кол.уч	Лист	№ док.	Подп.	Дата
Разраб.		Кырлан А.С.			21.10.26
Пров.					
ГИП					
Н. контр.					
Утв.					

ГД-2026-010-АИ

Дом 331 м²

Общая площадь 270,67* м² · * размеры приняты, не замерены (реестр — л. 7, К-1)

Дизайн-проект интерьера

Стадия	Лист	Листов
РП	91	159

Шкаф распашной С3

М 1:20

Кырлан Александр Сергеевич

выпуск 18.10.2026 № 9365d64cec · стр. 96 из 197

Система хранения Сп3

Холл мансарды (пом. 17) · вид из помещения · размеры в мм, отметки в м

ПРЕДВАРИТЕЛЬНО · не для производства работ · открыто пунктов: 6 (реестр — л. 7)

Общий вид

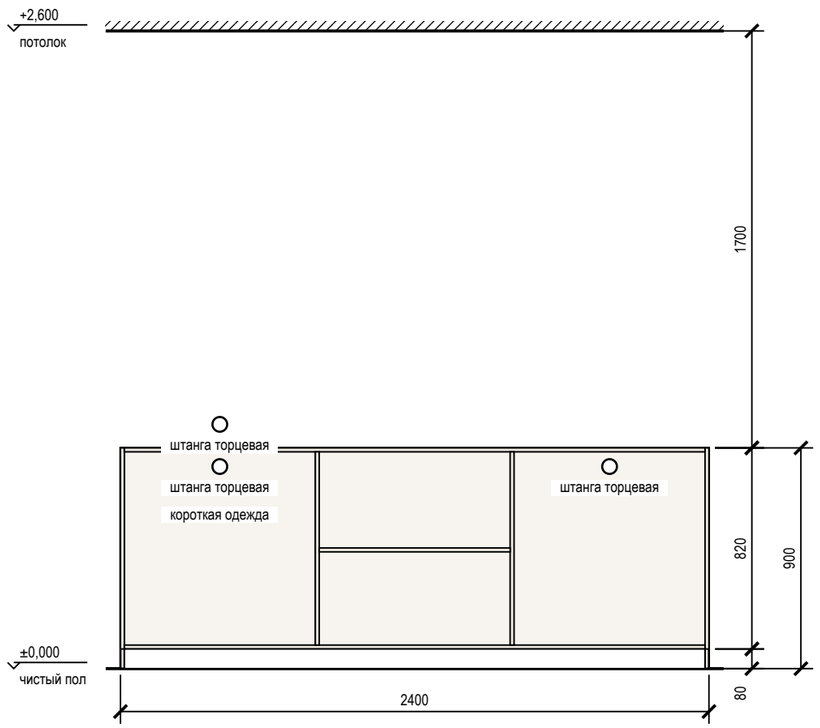

Наполнение, размеры в свету

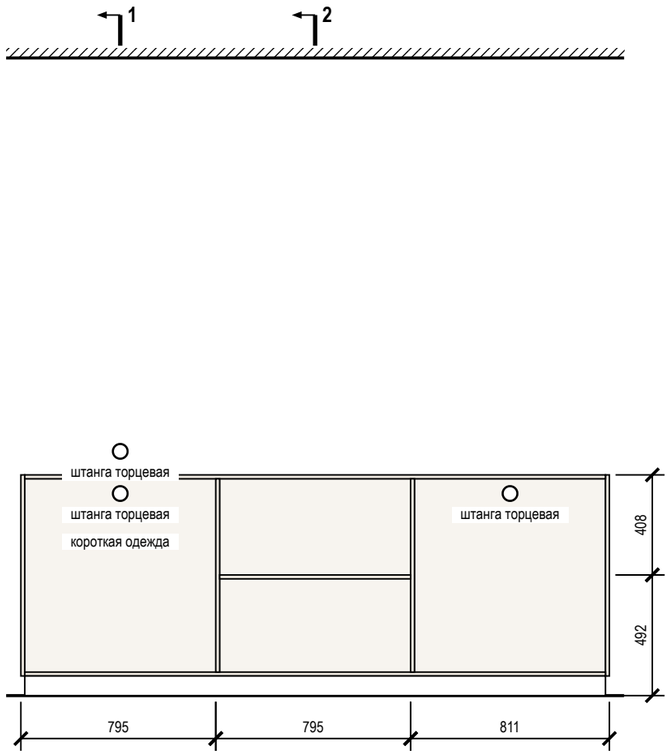

Разрез 1-1

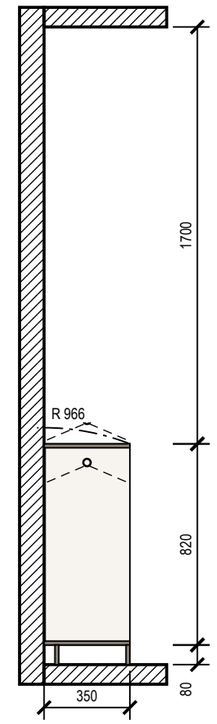

Разрез 2-2

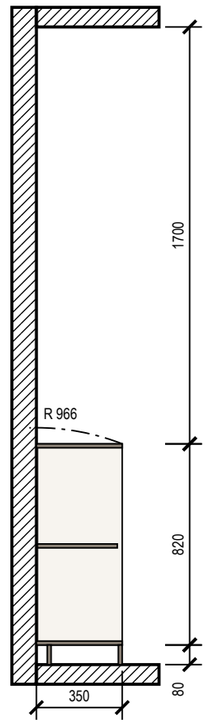

Примечания

1. Размеры — в мм по чистовой отделке; изделие 2400×350×900 (Ш×Г×В). Перед раскроем — контрольный замер цеха после чистовой отделки стен, пола и потолка.
2. Корпус — ЛДСП 16 мм, задняя стенка ХДФ 4 мм в паз, цоколь 80 мм на регулируемых опорах; открытая система без фасадов, ящики с фасадами.
3. Кромка: скрытые торцы 0,4 мм, видимые 2 мм (ПВХ/АБС).
4. Номинальные зазоры: между фасадами ящиков 3 мм, фасад ящика — стойка 2 мм.
5. Ящики — направляющие полного выдвижения NL 300 (внутренняя глубина 346 мм ≥ NL + 3); присадка по 32-й системе — выполняет цех.
6. Зазор до потолка 1700 мм.
7. Подъём корпуса: диагональ боковины $\sqrt{(900^2 + 350^2)} = 966$ мм < 2600 мм до потолка — корпус собирается лёжа и поднимается поворотом.
8. Крепление к стене от опрокидывания: true; основание стены и шаг анкеров — монтажная схема шкафов.

Условные обозначения

- корпус и полки ЛДСП (вид на стену)
- задняя стенка ХДФ
- деталь в разрезе
- штанга для плечиков (на разрезе — плечики 450 мм)
- траектория угла корпуса при подъёме в проектное положение

Допущения и предложения на листе

Основа листа: размеры и контуры этажей подобраны проектировщиком по составу помещений и площадям этажей с картинки 470 px (размеры на ней не читаются); обмер и исходный проект — задание (К-1); высоты: 1-й этаж 2800 мм, мансарда 2700 мм (горизонтальная часть) приняты; скаты кровли мансарды приняты по картинке: колено 1200 мм, уклон 45°, конёк вдоль длинной стороны; проект КР — задание (К-2); наружные стены 400 мм, перегородки 120 мм приняты (К-1); разрешённая мощность 15 кВт принята по типовым ТУ для частного дома (К-4); подрайон климата не задан — принят не северный (жилые от 2,5 м) (К-7).
См. лист открытых вопросов (лист 7, записи К-1, К-2, К-4, К-7).

1000 мм · печать 1:1

Изм.	Кол.уч	Лист	№ док.	Подп.	Дата
Разраб.		Кырлан А.С.			21.10.26
Пров.					
ГИП					
Н. контр.					
Утв.					

ГД-2026-010-АИ

Дом 331 м²

Общая площадь 270,67* м² · * размеры приняты, не замерены (реестр — л. 7, К-1)

Дизайн-проект интерьера

Стадия	Лист	Листов
РП	92	159

Система хранения Сп3

М 1:25

Кырлан Александр Сергеевич

выпуск 18.10.2026 № 9365d64cec · стр. 97 из 197

Шкаф распашной ДЗ

Спальня 3 (пом. 18) · вид из помещения · размеры в мм, отметки в м

ПРЕДВАРИТЕЛЬНО · не для производства работ · открыто пунктов: 6 (реестр — л. 7)

Вид с фасадами

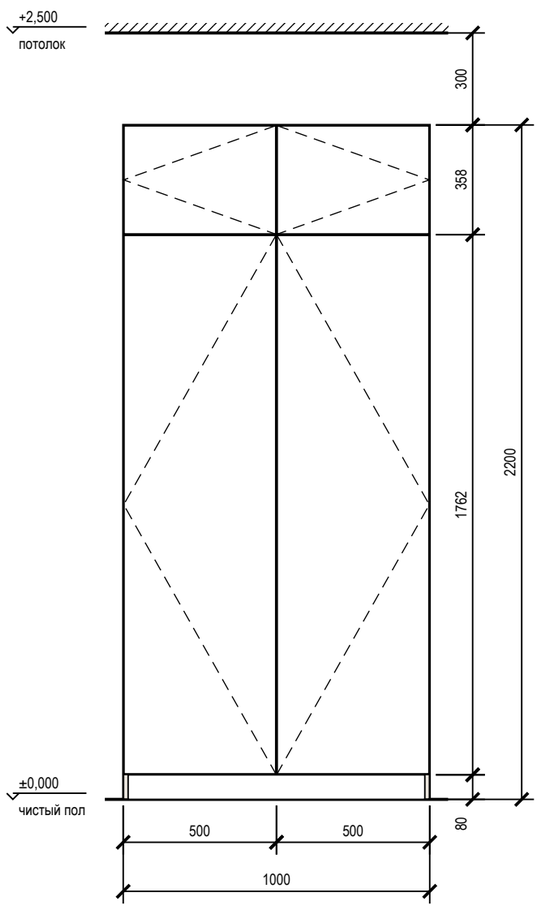

Вид без фасадов

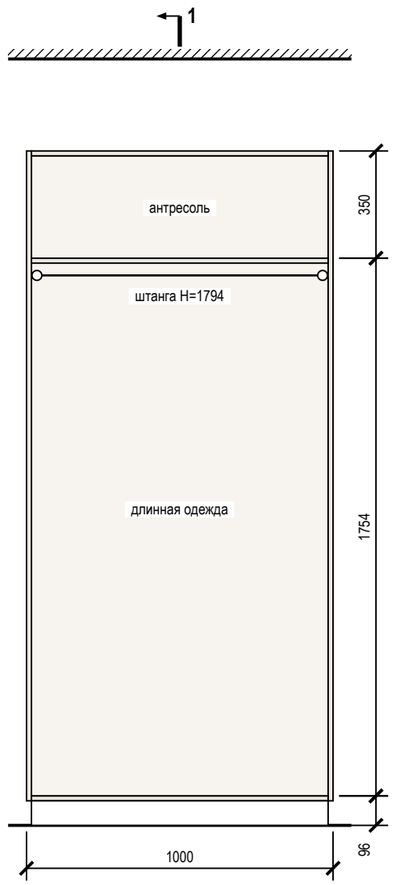

Разрез 1-1

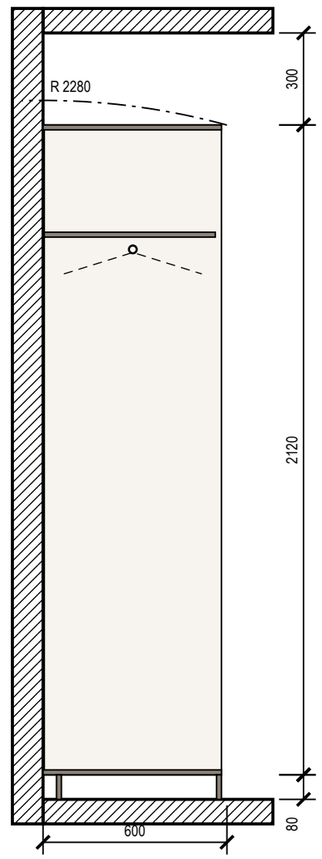

Примечания

1. Размеры — в мм по чистовой отделке; изделие 1000×600×2200 (Ш×Г×В). Перед раскроем — контрольный замер цеха после чистовой отделки стен, пола и потолка.
2. Корпус — ЛДСП 16 мм, задняя стенка ХДФ 4 мм в паз, цоколь 80 мм на регулируемых опорах; фасады — МДФ, эмаль матовая 18 мм накладные, цвет — по колерной карте; петли с доводчиком: фасад 1759 мм — 4 петли, фасад 355 мм — 2 петли.
3. Кромка: скрытые торцы 0,4 мм, видимые 2 мм (ПВХ/АБС).
4. Номинальные зазоры: между фасадами 3 мм, фасад — стена и фасад — потолок не менее 3 мм, фасад ящика — стойка 2 мм.
5. Ящики — направляющие полного выдвижения NL 550 (внутренняя глубина 578 мм ≥ NL + 3); присадка по 32-й системе — выполняет цех.
6. Зазор до потолка 300 мм.
7. Подъём корпуса: диагональ боковины $\sqrt{(2200^2 + 600^2)} = 2280$ мм < 2500 мм до потолка — корпус собирается лёжа и поднимается поворотом.
8. Крепление к стене от опрокидывания — уголки 2 шт. к несущему основанию (монтажная схема шкафов).

Условные обозначения

- фасад распашной: линии сходятся к стороне петель
- корпус и полки ЛДСП (вид на стену)
- задняя стенка ХДФ
- деталь в разрезе
- штанга для плечиков (на разрезе — плечики 450 мм)
- траектория угла корпуса при подъёме в проектное положение

Допущения и предложения на листе

Основа листа: размеры и контуры этажей подобраны проектировщиком по составу помещений и площадям этажей с картинки 470 px (размеры на ней не читаются); обмер и исходный проект — задание (К-1); высоты: 1-й этаж 2800 мм, мансарда 2700 мм (горизонтальная часть) приняты; скаты кровли мансарды приняты по картинке: колено 1200 мм, уклон 45°, конёк вдоль длинной стороны; проект КР — задание (К-2); наружные стены 400 мм, перегородки 120 мм приняты (К-1); разрешённая мощность 15 кВт принята по типовым ТУ для частного дома (К-4); подрайон климата не задан — принят не северный (жилые от 2,5 м) (К-7).
См. лист открытых вопросов (лист 7, записи К-1, К-2, К-4, К-7).

1000 мм · печать 1:1

Изм.	Кол.уч	Лист	№ док.	Подп.	Дата
Разраб.		Кырлан А.С.			21.10.26
Пров.					
ГИП					
Н. контр.					
Утв.					

ГД-2026-010-АИ

Дом 331 м²

Общая площадь 270,67* м² · * размеры приняты, не замерены (реестр — л. 7, К-1)

Дизайн-проект интерьера

Стадия	Лист	Листов
РП	93	159

Шкаф распашной ДЗ

М 1:20

Кырлан Александр Сергеевич

выпуск 18.10.2026 № 9365d64cec · стр. 98 из 197

Шкаф распашной Д6

Спальня 4 (пом. 19) · вид из помещения · размеры в мм, отметки в м

ПРЕДВАРИТЕЛЬНО · не для производства работ · открыто пунктов: 6 (реестр — л. 7)

Вид с фасадами

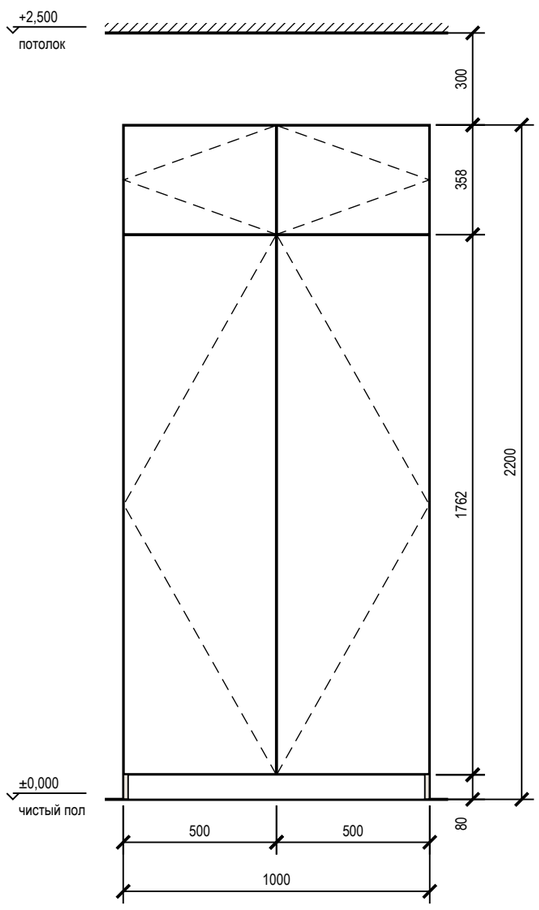

Вид без фасадов

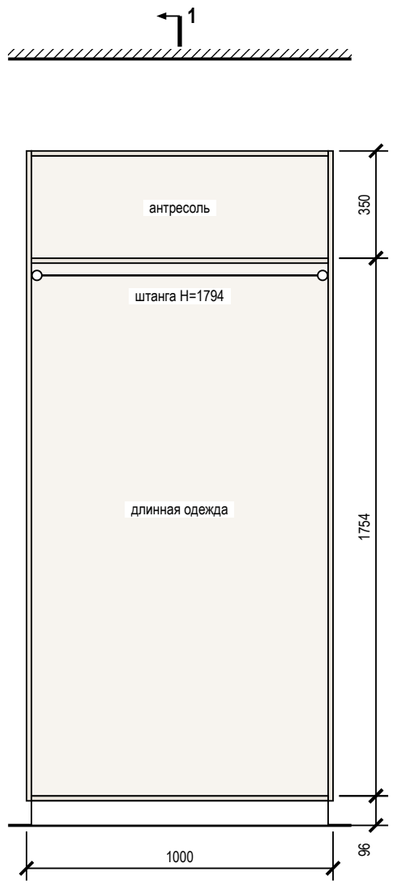

Разрез 1-1

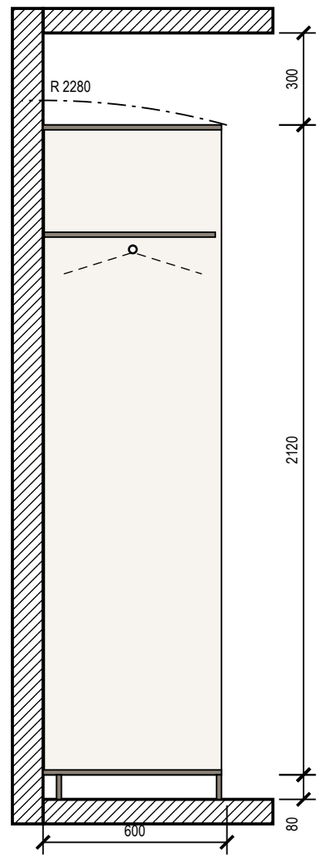

Примечания

1. Размеры — в мм по чистовой отделке; изделие 1000×600×2200 (Ш×Г×В). Перед раскроем — контрольный замер цеха после чистовой отделки стен, пола и потолка.
2. Корпус — ЛДСП 16 мм, задняя стенка ХДФ 4 мм в паз, цоколь 80 мм на регулируемых опорах; фасады — МДФ, эмаль матовая 18 мм накладные, цвет — по колерной карте; петли с доводчиком: фасад 1759 мм — 4 петли, фасад 355 мм — 2 петли.
3. Кромка: скрытые торцы 0,4 мм, видимые 2 мм (ПВХ/АБС).
4. Номинальные зазоры: между фасадами 3 мм, фасад — стена и фасад — потолок не менее 3 мм, фасад ящика — стойка 2 мм.
5. Ящики — направляющие полного выдвижения NL 550 (внутренняя глубина 578 мм ≥ NL + 3); присадка по 32-й системе — выполняет цех.
6. Зазор до потолка 300 мм.
7. Подъём корпуса: диагональ боковины $\sqrt{(2200^2 + 600^2)} = 2280$ мм < 2500 мм до потолка — корпус собирается лёжа и поднимается поворотом.
8. Крепление к стене от опрокидывания — уголки 2 шт. к несущему основанию (монтажная схема шкафов).

Условные обозначения

- фасад распашной: линии сходятся к стороне петель
- корпус и полки ЛДСП (вид на стену)
- задняя стенка ХДФ
- деталь в разрезе
- штанга для плечиков (на разрезе — плечики 450 мм)
- траектория угла корпуса при подъёме в проектное положение

Допущения и предложения на листе

Основа листа: размеры и контуры этажей подобраны проектировщиком по составу помещений и площадям этажей с картинки 470 px (размеры на ней не читаются); обмер и исходный проект — задание (К-1); высоты: 1-й этаж 2800 мм, мансарда 2700 мм (горизонтальная часть) приняты; скаты кровли мансарды приняты по картинке: колено 1200 мм, уклон 45°, конёк вдоль длинной стороны; проект КР — задание (К-2); наружные стены 400 мм, перегородки 120 мм приняты (К-1); разрешённая мощность 15 кВт принята по типовым ТУ для частного дома (К-4); подрайон климата не задан — принят не северный (жилые от 2,5 м) (К-7).
См. лист открытых вопросов (лист 7, записи К-1, К-2, К-4, К-7).

1000 мм · печать 1:1

Изм.	Кол.уч	Лист	№ док.	Подп.	Дата
Разраб.		Кырлан А.С.			21.10.26
Пров.					
ГИП					
Н. контр.					
Утв.					

ГД-2026-010-АИ

Дом 331 м²

Общая площадь 270,67* м² · * размеры приняты, не замерены (реестр — л. 7, К-1)

Дизайн-проект интерьера

Стадия	Лист	Листов
РП	94	159

Шкаф распашной Д6

М 1:20

Кырлан Александр Сергеевич

выпуск 18.10.2026 № 9365d64cec · стр. 99 из 197

Кухня (пом. 1). Развёртка гарнитура

Кухня-столовая (пом. 1) · стена А · вид из помещения · размеры в мм, отметки в м

Вид с фасадами

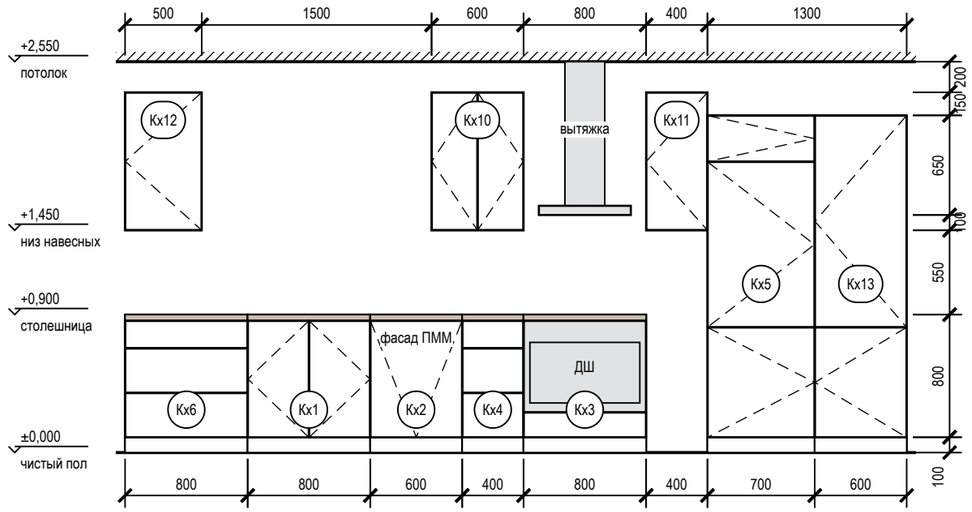

Вид без фасадов (наполнение, выводы)

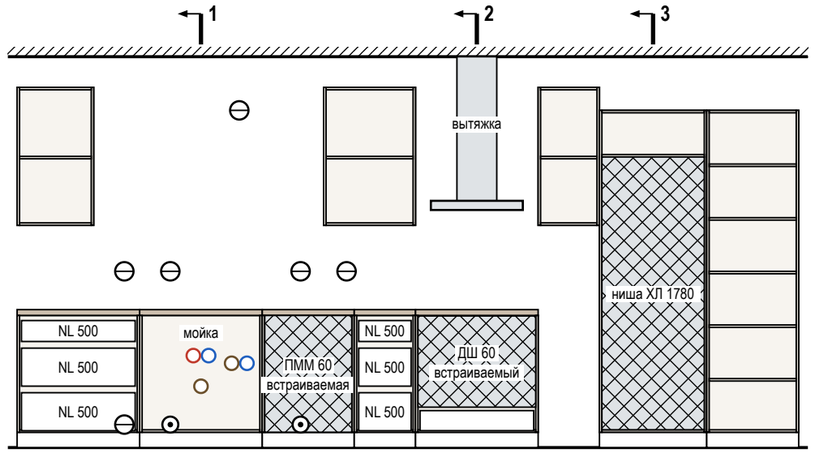

Разрез 1-1

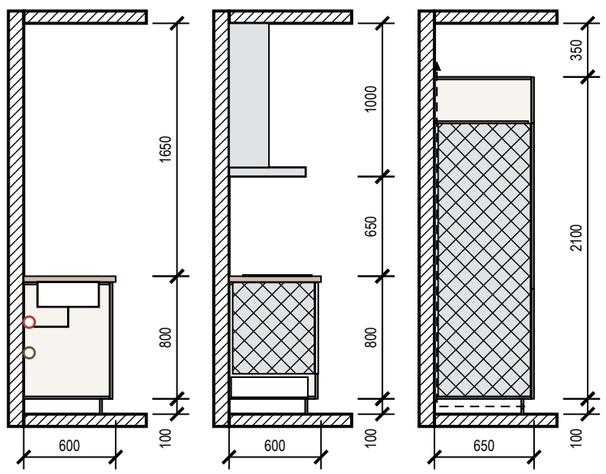

Разрез 2-2

Разрез 3-3

Условные обозначения

- фасад распашной: линии сходятся к стороне петель
- фасад ящика, карго
- встраиваемая техника
- столешница
- доборная планка
- деталь в разрезе
- К1 — марка модуля
- розетка на стене
- вывод кабеля к технике
- В1 — вывод воды В1 / Т3, канализации К1

Примечания

1. Размеры — в мм по чистовой отделке, вид из помещения; марки — как на плане расстановки. Перед раскроем — контрольный замер цеха после фартука и пола.
2. Корпуса — ЛДСП 16 мм, задняя стенка ХДФ 4 мм; фасады — МДФ, эмаль матовая 18 мм, цвет по колерной карте; столешница 38 мм, свес 20 мм; цоколь 100 мм.
3. Кромка: скрытые торцы 0,4 мм, видимые 2 мм. Номинальные зазоры: между фасадами 3 мм, фасад — столешница 3 мм, фасад — стена не менее 3 мм.
4. Ящики полного выдвижения и петли — с доводчиком; присадка по 32-й системе — выполняет цех.
5. Низ вытяжки — не ниже 650 мм над варочной панелью или по паспорту модели; короб воздуховода — до потолка.
6. Ниши техники (холодильник — ориентир 1780 мм) — по монтажным схемам выбранных моделей: решётка в цоколе и канал за пеналом холодильника, зазор за духовым шкафом, фасад ПММ на двери машины.

Допущения и предложения на листе

Основа листа: размеры и контуры этажей подобраны проектировщиком по составу помещений и площадям этажей с картинки 470 px (размеры на ней не читаются); обмер и исходный проект — задание (К-1); высоты: 1-й этаж 2800 мм, мансарда 2700 мм (горизонтальная часть) приняты; скаты кровли мансарды приняты по картинке: колено 1200 мм, уклон 45°, конёк вдоль длинной стороны; проект КР — задание (К-2); наружные стены 400 мм, перегородки 120 мм приняты (К-1); разрешённая мощность 15 кВт принята по типовым ТУ для частного дома (К-4); подрайон климата не задан — принят не северный (жилые от 2,5 м) (К-7).

См. лист открытых вопросов (лист 7, записи К-1, К-2, К-4, К-7).

1000 мм · печать 1:1

Изм.	Кол.уч	Лист	№ док.	Подп.	Дата
Разраб.		Кырлан А.С.			21.10.26
Пров.					
ГИП					
Н. контр.					
Утв.					

ГД-2026-010-АИ

Дом 331 м²

Общая площадь 270,67* м² · * размеры приняты, не замерены (реестр — л. 7, К-1)

Дизайн-проект интерьера

Стадия	Лист	Листов
РП	95	159

Кухня (пом. 1). Развёртка гарнитура

М 1:40

Кырлан Александр Сергеевич

выпуск 18.10.2026 № 9365d64cec · стр. 100 из 197

Кухня (пом. 1). Монтажная схема

Кухня-столовая (пом. 1) · стена А · размеры в мм от чистых поверхностей, высоты — от чистого пола

ПРЕДВАРИТЕЛЬНО · не для производства работ · открыто пунктов: 6 (реестр — л. 7)

Привязка выводов и крепление модулей

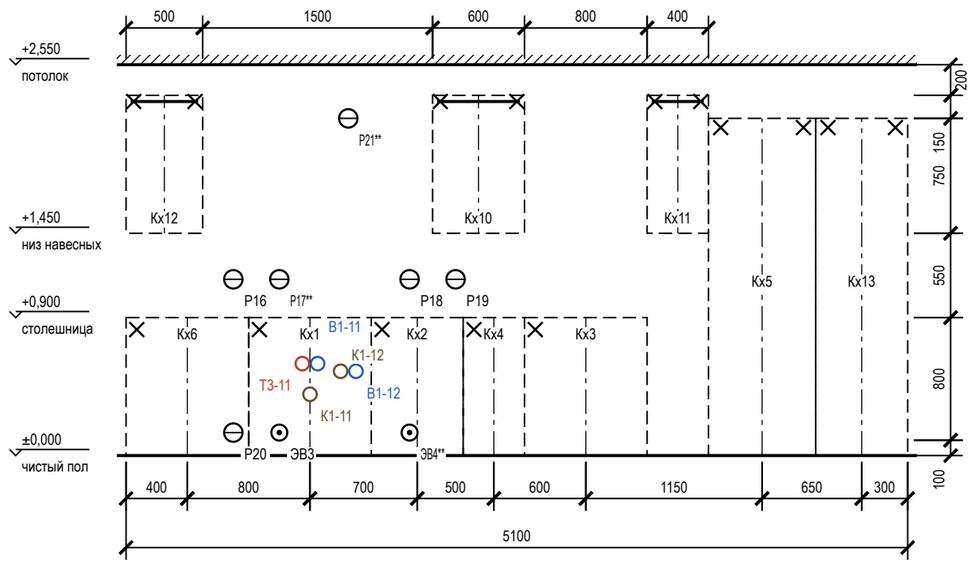

План столешницы

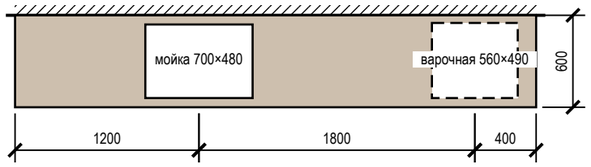

Примечания

1. Выводы — по проекту электрики и ВК; привязка по горизонтали — от оси модуля (плюс — вправо по виду), по высоте — от чистого пола до оси вывода.
2. Пенал — уголки к стене 2 шт. сверху; нижние модули — стяжками между собой и уголком к стене; ряд выставить по уровню опорами цоколя.
3. Розетки над столешницей — не ниже 150 мм над ней и не за корпусом техники; розетка за ПММ, духовым шкафом и холодильником — только в соседнем модуле или в зоне цоколя с доступом.
4. Столешница — вырезы по шаблонам выбранных моделей мойки и варочной панели; торцы у стены — герметик, пристеночный плинтус.

Привязка выводов к осям модулей

Код	Назначение	Модуль	От оси, мм	H, мм	Размещение
P16	розетка ×2 — фартук: мелкая техника	Кх6	+300	1150	над столешницей (фартук)
P20	розетка — холодильник встроенный M20 (розетка в модуле M21)	Кх6	+300	150	в соседнем модуле, за ящиком
P17**	розетка ×2 — фартук: мелкая техника	Кх1	−200	1150	над столешницей (фартук)
ЭВ3	вывод кабеля — варочная панель M22	Кх1	−200	150	в модуле мойки
T3-11	Т3 — межос. 100	Кх1	−50	600	в модуле мойки
K1-11	К1 Ø50 — мойка	Кх1	0	400	в модуле мойки
B1-11	В1 — межос. 100	Кх1	+50	600	в модуле мойки
K1-12	К1 Ø40 — слив ПММ в шкафу мойки	Кх1	+200	550	в модуле мойки
P21**	розетка — вытяжка M25 (в модуле, съёмная панель)	Кх1	+250	2200	над столешницей (фартук)
B1-12	В1 — кран ПММ в шкафу мойки	Кх1	+300	550	в модуле мойки
P18	розетка ×2 — фартук: мелкая техника	Кх2	−50	1150	над столешницей (фартук)
ЭВ4**	вывод кабеля — духовой шкаф M22 (вывод в соседнем модуле M23)	Кх2	−50	150	за ПММ — перенести в соседний модуль
P19	розетка ×2 — фартук: мелкая техника	Кх2	+250	1150	над столешницей (фартук)

Зазоры под отделку

Поверхность	Отделка	Зазор, мм	Учесть
фартук	керамогранит	10	от чернового основания до корпуса навесных и столешницы
стены	окраска	5	под штукатурку и шпаклёвку за пеналом
пол	инженерная доска		цоколь — после укладки пола, опоры ±20 мм

Условные обозначения

- навесной модуль (невидимый контур)
- ось модуля (от неё — привязка вывода)
- анкер / уголок крепления к стене
- розетка на стене
- вывод кабеля к технике
- B1 — вывод воды В1 / Т3, канализации К1

Допущения и предложения на листе

Основа листа: размеры и контуры этажей подобраны проектировщиком по составу помещений и площадям этажей с картинки 470 px (размеры на ней не читаются); обмер и исходный проект — задание (К-1); высоты: 1-й этаж 2800 мм, мансарда 2700 мм (горизонтальная часть) приняты; скаты кровли мансарды приняты по картинке: колено 1200 мм, уклон 45°, конёк вдоль длинной стороны; проект КР — задание (К-2); наружные стены 400 мм, перегородки 120 мм приняты (К-1); разрешённая мощность 15 кВт принята по типовым ТУ для частного дома (К-4); подрайон климата не задан — принят не северный (жилые от 2,5 м) (К-7).

Знак «**» — предложение проектировщика, заказчиком не утверждено (согласовать с заказчиком): записи в реестре нет: P21 — высота 2200 мм выше нормы 1 м (ПУЭ 6.6.30) по назначению: питание вытяжки M25, розетка в модуле за съёмной панелью; ЭВ4 — по образцу: Добавлены выводы к вентиляторам: ЭВ4 (ВР1, ванная) и ЭВ5 (ВР3, санузел 2) — группа 3, высота 2389 мм, включение с основным светом, таймер выбега в вентиляторе; и коробки уравнивания потенциалов КУП1 (ванная) и КУП2 (санузел 2) — высота 300 мм, у входа, вне зон 0–2, проводник от шины PE щита ЩК, сече; P17 — высота 1700 мм выше нормы 1 м (ПУЭ 6.6.30) по назначению: питание слаботочного щита ЩС, рядом со щитом на его высоте. См. лист открытых вопросов (лист 7, записи К-1, К-2, К-4, К-7).

1000 мм · печать 1:1

Изм.	Кол.уч	Лист	№ док.	Подп.	Дата
Разраб.		Кырлан А.С.			21.10.26
Пров.					
ГИП					
Н. контр.					
Утв.					

ГД-2026-010-АИ

Дом 331 м²

Общая площадь 270,67* м² · * размеры приняты, не замерены (реестр — л. 7, К-1)

Дизайн-проект интерьера

Стадия	Лист	Листов
РП	96	159

Кухня (пом. 1). Монтажная схема

М 1:40

Кырлан Александр Сергеевич

выпуск 18.10.2026 № 9365d64cec · стр. 101 из 197

Шкафы. Монтажная схема. Лист 1 из 2

крепление к стене, установочные размеры, зазоры под отделку · размеры в мм

ПРЕДВАРИТЕЛЬНО · не для производства работ · открыто пунктов: 6 (реестр — л. 7)

Система хранения Кт1 (пом. 4)

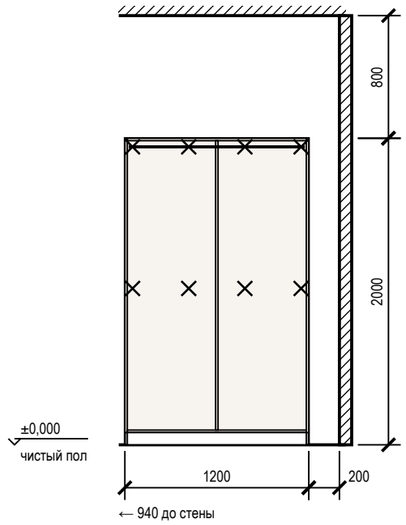

Система хранения Кл1 (пом. 7)

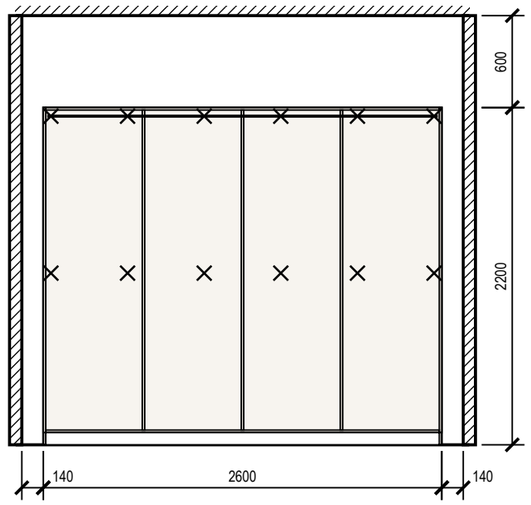

Шкаф-купе Пр1 (пом. 8)

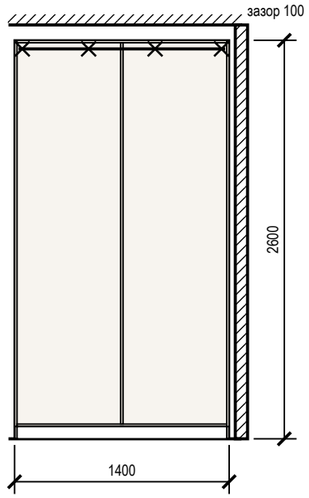

Система хранения Гр1 (пом. 10)

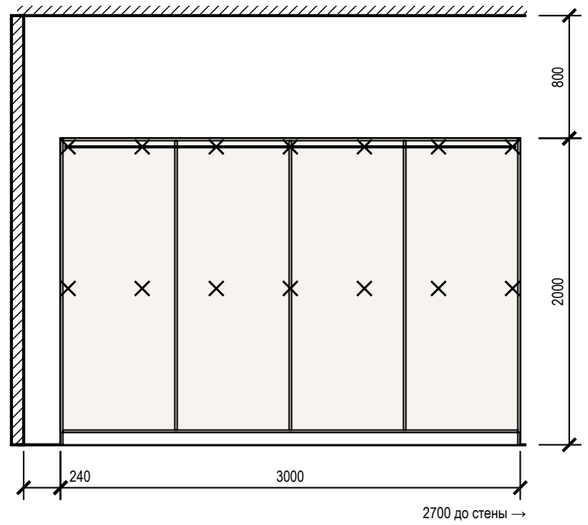

Крепление и зазоры под отделку (изделия листа 1)

Марка	Помещение, стена	Основание	Отделка стены	Зазор, мм	Крепёж по планке	От опрокидывания
Кт1	Котельная (4), стена Г	по основанию — см. таблицу крепежа	окраска	5	анкер 8 шт. (2 ряда)	уголки 2 шт.
Кл1	Кладовая (7), стена В	по основанию — см. таблицу крепежа	окраска	5	анкер 12 шт. (2 ряда)	уголки 2 шт.
Пр1	Прихожая (8), стена А	по основанию — см. таблицу крепежа	окраска	5	анкер 4 шт., шаг 433	уголки 2 шт.
Гр1	Гараж (10), стена А	по основанию — см. таблицу крепежа	окраска	5	анкер 14 шт. (2 ряда)	true

Крепёж по основанию стены

Основание стены	Крепёж
бетон, ж/б	анкер-шуруп 7,5×72 или дюбель 8×60 с шурупом 5×70
кирпич полнотелый	дюбель 8×80 с шурупом 5×90
газобетон, пазогребень	дюбель для газобетона 10×100 или химический анкер
гипсокартон	закладная до обшивки (брус 40×80 или фанера 18 мм), саморез в закладную

Условные обозначения

- анкер / уголок крепления к стене
- корпус и полки ЛДСП (вид на стену)
- компенсатор — короб до потолка

Примечания

1. Установочные размеры — от чистого пола и чистых стен; перед установкой контрольный замер после отделки.
2. Порядок: корпус выставить по уровню опорами цоколя → закрепить к стене по задней планке → навесить двери и фасады, отрегулировать зазоры → подогнать и закрепить компенсатор.
3. Анкеры — с шагом не более 500 мм, не ближе 50 мм от края планки; на ГКЛ только в закладную, установленную до обшивки.
4. Скрытые коммуникации под анкеры проверить детектором; трассы электрики по плану розеток.
5. Монтажная схема на 2 листах, лист 1 из 2; продолжение — на следующем листе схемы. Условные обозначения, таблица крепежа по основанию и примечания повторены на каждом листе.

Допущения и предложения на листе

Основа листа: размеры и контуры этажей подобраны проектировщиком по составу помещений и площадям этажей с картинки 470 px (размеры на ней не читаются); обмер и исходный проект — задание (К-1); высоты: 1-й этаж 2800 мм, мансарда 2700 мм (горизонтальная часть) приняты; скаты кровли мансарды приняты по картинке: колено 1200 мм, уклон 45°, конёк вдоль длинной стороны; проект КР — задание (К-2); наружные стены 400 мм, перегородки 120 мм приняты (К-1); разрешённая мощность 15 кВт принята по типовым ТУ для частного дома (К-4); подрайон климата не задан — принят не северный (жилые от 2,5 м) (К-7).

См. лист открытых вопросов (лист 7, записи К-1, К-2, К-4, К-7).

1000 мм · печать 1:1

Изм.	Кол.уч	Лист	№ док.	Подп.	Дата
Разраб.		Кырлан А.С.			21.10.26
Пров.					
ГИП					
Н. контр.					
Утв.					

ГД-2026-010-АИ

Дом 331 м²

Общая площадь 270,67* м² · * размеры приняты, не замерены (реестр — л. 7, К-1)

Дизайн-проект интерьера	Стадия	Лист	Листов
	РП	97	159

Шкафы. Монтажная схема. Лист 1 из 2

М 1:40

Кырлан Александр Сергеевич

выпуск 18.10.2026 № 9365d64cec · стр. 102 из 197

Шкафы. Монтажная схема. Лист 2 из 2

крепление к стене, установочные размеры, зазоры под отделку · размеры в мм

ПРЕДВАРИТЕЛЬНО · не для производства работ · открыто пунктов: 6 (реестр — л. 7)

Система хранения Гм2 (пом. 14)

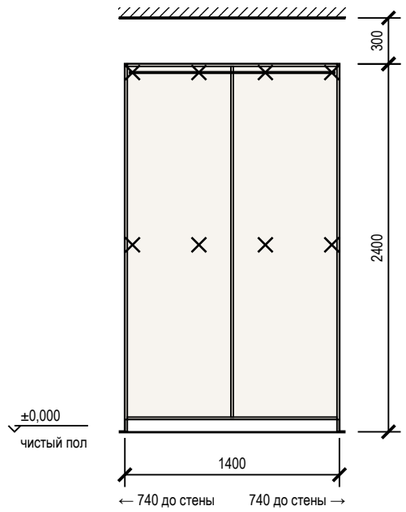

Шкаф распашной С3 (пом. 16)

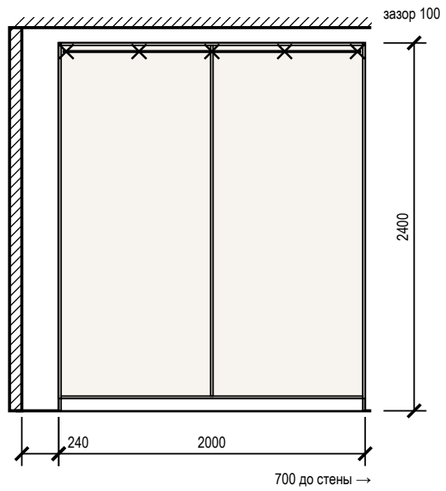

Система хранения Сп3 (пом. 17)

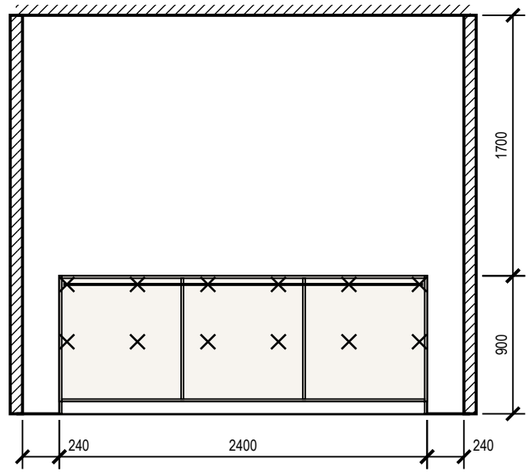

Шкаф распашной Д3 (пом. 18)

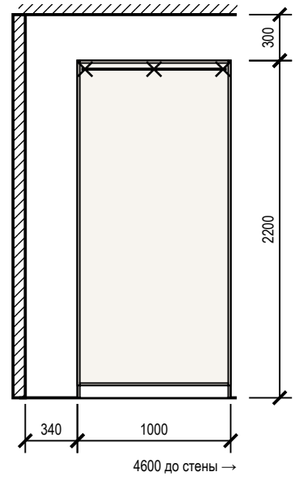

Шкаф распашной Д6 пом. 19

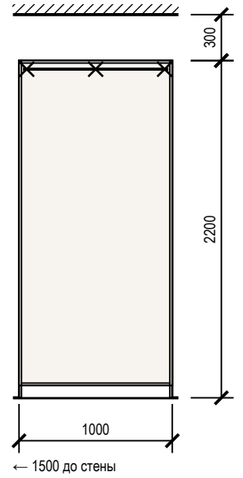

Крепление и зазоры под отделку (изделия листа 2)

Марка	Помещение, стена	Основание	Отделка стены	Зазор, мм	Крепёж по планке	От опрокидывания
Гм2	Гардеробная мастер (14), стена В	по основанию — см. таблицу крепежа	окраска	5	анкер 8 шт. (2 ряда)	уголки 2 шт.
С3	Спальня 2 (16), стена А	по основанию — см. таблицу крепежа	окраска	5	анкер 5 шт., шаг 475	уголки 2 шт.
Сп3	Холл мансарды (17), стена В	по основанию — см. таблицу крепежа	окраска	5	анкер 12 шт. (2 ряда)	true
Д3	Спальня 3 (18), стена В	по основанию — см. таблицу крепежа	окраска	5	анкер 3 шт., шаг 450	уголки 2 шт.
Д6	Спальня 4 (19), стена А	по основанию — см. таблицу крепежа	окраска	5	анкер 3 шт., шаг 450	уголки 2 шт.

Крепёж по основанию стены

Основание стены	Крепёж
бетон, ж/б	анкер-шуруп 7,5×72 или дюбель 8×60 с шурупом 5×70
кирпич полнотелый	дюбель 8×80 с шурупом 5×90
газобетон, пазогребень	дюбель для газобетона 10×100 или химический анкер
гипсокартон	закладная до обшивки (брус 40×80 или фанера 18 мм), саморез в закладную

Условные обозначения

- анкер / уголок крепления к стене
- корпус и полки ЛДСП (вид на стену)
- компенсатор — короб до потолка

Примечания

1. Установочные размеры — от чистого пола и чистых стен; перед установкой контрольный замер после отделки.
2. Порядок: корпус выставить по уровню опорами цоколя → закрепить к стене по задней планке → навесить двери и фасады, отрегулировать зазоры → подогнать и закрепить компенсатор.
3. Анкеры — с шагом не более 500 мм, не ближе 50 мм от края планки; на ГКЛ только в закладную, установленную до обшивки.
4. Скрытые коммуникации под анкеры проверить детектором; трассы электрики по плану розеток.
5. Монтажная схема на 2 листах, лист 2 из 2. Условные обозначения, таблица крепежа по основанию и примечания повторены на каждом листе.

Допущения и предложения на листе

Основа листа: размеры и контуры этажей подобраны проектировщиком по составу помещений и площадям этажей с картинки 470 px (размеры на ней не читаются); обмер и исходный проект — задание (К-1); высоты: 1-й этаж 2800 мм, мансарда 2700 мм (горизонтальная часть) приняты; скаты кровли мансарды приняты по картинке: колено 1200 мм, уклон 45°, конёк вдоль длинной стороны; проект КР — задание (К-2); наружные стены 400 мм, перегородки 120 мм приняты (К-1); разрешённая мощность 15 кВт принята по типовым ТУ для частного дома (К-4); подрайон климата не задан — принят не северный (жилые от 2,5 м) (К-7).
См. лист открытых вопросов (лист 7, записи К-1, К-2, К-4, К-7).

1000 мм · печать 1:1

Изм.	Кол.уч	Лист	№ док.	Подп.	Дата
Разраб.		Кырлан А.С.			21.10.26
Пров.					
ГИП					
Н. контр.					
Утв.					

ГД-2026-010-АИ

Дом 331 м²

Общая площадь 270,67* м² · * размеры приняты, не замерены (реестр — л. 7, К-1)

Дизайн-проект интерьера

Стадия	Лист	Листов
РП	98	159

Шкафы. Монтажная схема. Лист 2 из 2

М 1:40

Кырлан Александр Сергеевич

выпуск 18.10.2026 № 9365d64cec · стр. 103 из 197

Ведомости изделий, техники и фурнитуры

встроенная мебель и кухонный гарнитур · размеры в мм

Ведомость изделий

Марка	Наименование	Пом.	Ш×Г×В, мм	Корпус	Фасад	Кромка, мм скр./вид.	Кол.
Кт1	Система хранения	4	1200×400×2000	ЛДСП 16	без фасадов; ящики — МДФ 18, эмаль матовая	0,4 / 2	1
Кл1	Система хранения	7	2600×500×2200	ЛДСП 16	без фасадов; ящики — МДФ 18, эмаль матовая	0,4 / 2	1
Пр1	Шкаф-купе	8	1400×600×2600	ЛДСП 16	рифлёные панели МДФ в алюминиевом профиле	0,4 / 2	1
Гр1	Система хранения	10	3000×500×2000	ЛДСП 16	без фасадов; ящики — МДФ 18, эмаль матовая	0,4 / 2	1
Гм2	Система хранения	14	1400×500×2400	ЛДСП 16	без фасадов; ящики — МДФ 18, эмаль матовая	0,4 / 2	1
С3	Шкаф распашной	16	2000×600×2400	ЛДСП 16	МДФ 18, эмаль матовая	0,4 / 2	1
Сп3	Система хранения	17	2400×350×900	ЛДСП 16	без фасадов; ящики — МДФ 18, эмаль матовая	0,4 / 2	1
Д3	Шкаф распашной	18	1000×600×2200	ЛДСП 16	МДФ 18, эмаль матовая	0,4 / 2	1
Д6	Шкаф распашной	19	1000×600×2200	ЛДСП 16	МДФ 18, эмаль матовая	0,4 / 2	1
Кх6	Модуль нижний: ящики	1	800×600×900	ЛДСП 16	МДФ 18, эмаль матовая	0,4 / 2	1
Кх12	Модуль навесной: полки	1	500×350×900	ЛДСП 16	МДФ 18, эмаль матовая	0,4 / 2	1
Кх1	Модуль нижний: мойка	1	800×600×900	ЛДСП 16	МДФ 18, эмаль матовая	0,4 / 2	1
Кх2	Модуль нижний: ПММ	1	600×600×900	ЛДСП 16	МДФ 18, эмаль матовая	0,4 / 2	1
Кх10	Модуль навесной: полки	1	600×350×900	ЛДСП 16	МДФ 18, эмаль матовая	0,4 / 2	1
Кх4	Модуль нижний: ящики	1	400×600×900	ЛДСП 16	МДФ 18, эмаль матовая	0,4 / 2	1
Кх3	Модуль нижний: духовой шкаф, варочная	1	800×600×900	ЛДСП 16	МДФ 18, эмаль матовая	0,4 / 2	1
Кх11	Модуль навесной: полки	1	400×350×900	ЛДСП 16	МДФ 18, эмаль матовая	0,4 / 2	1
Кх5	Пенал: холодильник встр.	1	700×650×2200	ЛДСП 16	МДФ 18, эмаль матовая	0,4 / 2	1
Кх13	Пенал: полки	1	600×600×2200	ЛДСП 16	МДФ 18, эмаль матовая	0,4 / 2	1

Ведомость встраиваемой техники

Поз.	Прибор	Ниша, вырез, мм	Вентиляция	Питание	Схема
Кх1	Мойка врезная / подстольная с сифоном	вырез по шаблону, ориентир 700 × 480		смеситель — выводы ВК	по модели
Кх2	Посудомоечная машина встраиваемая, 60 см	ниша 600 × 862 (от пола до низа столешницы)	зазор в цоколе, по схеме	розетка в соседнем модуле	по модели
Кх3	Духовой шкаф встраиваемый, 60 см	ниша 560 × 595, глубина ≥ 550	зазор за шкафом, вырез в задней стенке	вывод кабеля под шкафом	по модели
Кх3	Варочная панель индукционная, 60 см	вырез в столешнице 560 × 490		вывод кабеля под модулем	по модели
Кх5	Холодильник встраиваемый, ниша 1780	ниша 1780 × 560 × 550	решётка в цоколе, канал за корпусом, выход сверху	розетка над нишей или в соседнем модуле	по модели
Кх3	Вытяжка настенная, 60 см	низ ≥ 650 над панелью	воздуховод к вентканалу, короб до потолка	вывод кабеля в коробе	по модели

Ведомость фурнитуры

№	Фурнитура	Тип, размер	Изделия	Кол.
1	Штанга выдвижная торцевая	L по глубине	Кт1, Кл1, Гр1, Гм2, Сп3	9
2	Полкодержатель с фиксацией	ø5 мм	Кт1, Кл1, Пр1, Гр1, Гм2, С3, Сп3, Д3, Д6, Кх12, Кх10, Кх11, Кх5, Кх13	220
3	Опора регулируемая с цоколем на клипсах	ход 20 мм	Кт1, Кл1, Пр1, Гр1, Гм2, С3, Сп3, Д3, Д6	66
4	Анкер по основанию стены	по таблице крепежа	Кт1, Кл1, Пр1, Гр1, Гм2, С3, Сп3, Д3, Д6, Кх12, Кх10, Кх11	75
5	Уголок крепления к стене от опрокидывания	стальной	Кт1, Кл1, Пр1, Гр1, Гм2, С3, Сп3, Д3, Д6, Кх5, Кх13	22
6	Система дверей купе: профиль, направляющие, ролики	на 2 двери	Пр1	1
7	Ручка-профиль вертикальная	в цвет профиля	Пр1	2
8	Штанга овальная 30×15, L = 676	+ 2 держателя	Пр1	1
9	Полка для обуви выдвижная наклонная	ширина 676	Пр1	3
10	Петля накладная 110° с доводчиком	чашка 35 мм	С3, Д3, Д6, Кх12, Кх1, Кх10, Кх11, Кх5, Кх13	72
11	Штанга овальная 30×15, L = 976	+ 2 держателя	С3	1
12	Штанга овальная 30×15, L = 968	+ 2 держателя	Д3, Д6	2
13	Направляющие полного выдвижения с доводчиком NL 500	пара	Кх6, Кх4, Кх3	7
14	Ручка-профиль	латунь матовая	Кх6, Кх12, Кх1, Кх2, Кх10, Кх4, Кх3, Кх11, Кх5, Кх13	19
15	Опора кухонная регулируемая 100–120 мм	+ клипса цоколя	Кх6, Кх1, Кх2, Кх4, Кх3, Кх5, Кх13	36
16	Навес регулируемый для навесного шкафа	пара на секцию	Кх12, Кх10, Кх11	3
17	Шина монтажная	L = 440	Кх12	1
18	Комплект навески фасада ПММ	из поставки машины	Кх2	1
19	Шина монтажная	L = 540	Кх10	1
20	Шина монтажная	L = 340	Кх11	1

Примечания

1. Модели техники выбирает заказчик до изготовления мебели; ниши, вырезы и вентиляция — по монтажной схеме выбранной модели (условие гарантии), её номер вносится в ведомость.
2. Количество фурнитуры — по чертежам изделий; запас крепежа 5 %. Аналоги — по характеристикам (доводчик, нагрузка, ход).
3. Цвет корпусов, фасадов и профилей — по колерной карте проекта.

Допущения и предложения на листе

Основа листа: размеры и контуры этажей подобраны проектировщиком по составу помещений и площадям этажей с картинки 470 px (размеры на ней не читаются); обмер и исходный проект — задание (К-1); высоты: 1-й этаж 2800 мм, мансарда 2700 мм (горизонтальная часть) приняты; скаты кровли мансарды приняты по картинке: колено 1200 мм, уклон 45°, конёк вдоль длинной стороны; проект КР — задание (К-2); наружные стены 400 мм, перегородки 120 мм приняты (К-1); разрешённая мощность 15 кВт принята по типовым ТУ для частного дома (К-4); подрайон климата не задан — принят не северный (жилые от 2,5 м) (К-7).
См. лист открытых вопросов (лист 7, записи К-1, К-2, К-4, К-7).

Изм.	Кол.уч	Лист	№ док.	Подп.	Дата
Разраб.		Кырлан А.С.			21.10.26
Пров.					
ГИП					
Н. контр.					
Утв.					

ГД-2026-010-АИ

Дом 331 м²

Общая площадь 270,67* м² · * размеры приняты, не замерены (реестр — л. 7, К-1)

Дизайн-проект интерьера

Стадия	Лист	Листов
РП	99	159

Ведомости изделий, техники и фурнитуры

М б/м

Кырлан Александр Сергеевич

04

Развёртки и узлы

Кырлан Александр Сергеевич

выпуск 18.10.2026 № 9365d64cec · стр. 105 из 197

Реестр марок отделки и позиций альбома

Реестр марок отделки (О ↔ позиции колерной карты) и марки позиций по видам

Реестр марок отделки альбома

Марка	Поверхность	Материал, изделие	Цвет, код	Помещения	Колер. карта
О1	стены	окраска, Tikkurila Luja 7, шелковисто-матовая, подготовка К3	NCS S 0804-Y30R «S 0804-Y30R»	1, 11, 12	К1
О2	фартук	керамогранит, аналог: керамогранит матовый, тон F497, затирка CG2WA	#F1F1EC «тон Paper F497»	1	КМ2
О3	плинтус	плинтус МДФ, h 80 мм, аналог: плинтус МДФ под окраску 80×16 мм, полуглянцевая	NCS S 0804-Y30R «S 0804-Y30R»	1, 5	К3
О4	потолок	окраска, Tikkurila Luja 7, матовая, подготовка Q3	NCS S 0804-Y30R «S 0804-Y30R»	1, 11, 12	К2
О5	пол	инженерная доска, Coswick Вековые традиции, 2100×127 мм, 1167-4250		1, 2, 5, 6, 7, 13, 14, 16, 17, 18, 19	КМ1
О6	стены	окраска, Farrow & Ball Modern Emulsion, матовая, подготовка Q3	Farrow & Ball No. 226 «Joa's White»	2, 4, 6, 8, 9, 10, 13, 16, 17, 18, 19	К4
О7	акцентная стена	окраска, Farrow & Ball Modern Emulsion, матовая, подготовка Q3	Farrow & Ball No. 298 «Bancha»	2	К5
О8	плинтус	плинтус МДФ, h 80 мм, аналог: плинтус МДФ под покраску 80×16	Farrow & Ball No. 226 «Joa's White»	2, 4, 6, 8, 9, 13, 16, 17	К7
О9	потолок	окраска, Tikkurila Anti-Reflex 2, глубокоматовая, подготовка Q3	Little Greene No. 105 «Slaked Lime»	2, 4, 6, 7, 8, 9, 10, 13, 14, 16, 17, 18, 19	К6
О10	стены	облицовка плиткой, Atlas Concorde Marvel Travertine, 600×1200×9 мм, A8UZ, затирка CG2WA	Atlas Concorde A8UZ «Marvel Travertine»	3, 15, 20	К8
О11	потолок	окраска, Tikkurila Luja 7, матовая, подготовка Q3	Little Greene No. 105 «Slaked Lime»	3, 15, 20	К9
О12	пол	керамогранит, Atlas Concorde Marvel Travertine, 600×1200×9 мм, A8UZ, затирка CG2WA	Atlas Concorde A8UZ «Marvel Travertine»	3, 4, 8, 9, 15, 20	К8
О13	стены	окраска, Tikkurila Optiva 5 Matt, матовая, подготовка К3	NCS S 0804-Y30R «S 0804-Y30R»	5	К10
О14	акцентная стена	окраска, Tikkurila Optiva 5 Matt, аналог: интерьерная краска, класс 2 по EN 13300, глубокоматовая/матовая, база C, матовая, подготовка К3	Farrow & Ball No. 93 «Studio Green — почти чёрный зелёный»	5	К11
О15	потолок	окраска, Tikkurila Anti-Reflex 2, глубокоматовая, подготовка Q3	NCS S 0804-Y30R «S 0804-Y30R»	5	К12
О16	стены	окраска, Tikkurila Harmony, матовая, подготовка Q3	Little Greene No. 105 «Slaked Lime»	7, 14	К13
О17	плинтус	плинтус МДФ, h 80 мм, аналог: плинтус МДФ под покраску 80×16	Little Greene No. 105 «Slaked Lime»	7, 14	К14
О18	плинтус	плинтус ПВХ, h 100 мм, аналог: плинтус ПВХ влагостойкий 100 мм, серый		10	КМ4
О19	пол	ероху, аналог: наливной полимерный пол (эпоксидный), с кварцевой посыпкой, 3 мм		10	КМ3
О20	плинтус	керамогранит, аналог: плинтус из керамогранита пола, подрезка 80 мм, верхняя кромка с запилом 45°	#B8AFA5 «тон Claystone V486»	11, 12	КМ6
О21	пол	керамогранит, Atlas Concorde Marvel Travertine, 600×1200×10 мм, A8UZ, затирка CG2WA	#B8AFA5 «тон Claystone V486»	11, 12	КМ5

Допущения и предложения на листе. Знак «**» предложено (согласовать): плинтус пом. 1, 2, 4–14, 16, 17, фартук пом. 1, акцент пом. 5, пол пом. 10. См. лист открытых вопросов (лист 7).

Реестр марок отделки альбома (продолжение)

Марка	Поверхность	Материал, изделие	Цвет, код	Помещения	Колер. карта
О22	акцентная стена	окраска, Farrow & Ball Modern Emulsion, матовая, подготовка Q3	NCS S 7020-G10Y «Хвойный тёмно-зелёный»	13	К15
О23	акцентная стена	окраска, Farrow & Ball Modern Emulsion, матовая, подготовка Q3	Farrow & Ball No. 64 «Red Earth»	16	К16
О24	акцентная стена	окраска, Farrow & Ball Modern Emulsion, матовая, подготовка Q3	NCS S 3020-G30Y «S 3020-G30Y»	18	К17
О25	плинтус	плинтус МДФ, Orac Decor Contour (Luxxus), h 69 мм, SX165	Farrow & Ball No. 226 «Joa's White»	18, 19	К18
О26	акцентная стена	окраска, Farrow & Ball Modern Emulsion, матовая, подготовка Q3	NCS S 3040-Y70R «S 3040-Y70R»	19	К19

Марки позиций альбома по видам

Префикс	Что обозначает, позиции	Листы
В, Д, Д-вх	двери: В-1, Д-1–Д-14, Д-вх	15–21
Пр	проёмы без полотна (порталы): Пр-1–Пр-3	15–21
ОК	окна: ОК-1–ОК-7	15–21
Вр, Гм, Гр, Гс, Д, Кб, Кл, Кт, Кх, М, Пр, С, Сп	мебель и оборудование: Вр1, Вр2, Вр4–Вр6, Гм1, Гм2, Гр1–Гр6, Гс1–Гс6, Д1–Д6, Кб1–Кб4, Кл1, Кт1, Кх1–Кх8, Кх10–Кх13, М1–М5, Пр1, Пр2, С1–С3, Сп1–Сп4	22–30
Сд, См, Сн	сантехнические приборы: Сд1–Сд4, См1–См4, Сн1–Сн4	49–53
ДК	декор (картины, зеркала, растения): ДК1–ДК13, ДК21–ДК28, ДК30, ДК31	1, 77–83
Т	текстиль (шторы, ковры): Т1–Т37, Т40, Т41	1, 77–83
Р	розетки: Р1–Р6, Р7**, Р8**, Р9–Р11, Р12**, Р13–Р16, Р17**, Р18–Р20, Р21**, Р22–Р26, Р33**, Р34, Р35, Р36**, Р37**, Р38**	31–44
ЭВ	выводы кабеля: ЭВ3, ЭВ4**, ЭВ5**, ЭВ6**, ЭВ7**, ЭВ9**	31–44
S	выключатели: S1, S2**, S3–S10, S14–S20	31–44
Св	светильники: Св1–Св40, Св50–Св58	31–44
БП	блоки питания LED: БП1–БП9	31–44
ИП	извещатели: ИП1–ИП4, ИП6	31–44
ТВ	розетки ТВ: ТВ1, ТВ2	31–44

Изм.	Кол.уч	Лист	№ док.	Подп.	Дата
Разраб.		Кырлан А.С.			21.10.26
Пров.					
ГИП					
Н. контр.					
Утв.					

ГД-2026-010-АИ

Дом 331 м²

Общая площадь 270,67* м² · * размеры приняты, не замерены (реестр — л. 7, К-1)

Дизайн-проект интерьера

Стадия	Лист	Листов
РП	100	159

Реестр марок отделки и позиций альбома

М б/м

Кырлан Александр Сергеевич

выпуск 18.10.2026 № 9365d64cec · стр. 106 из 197

Реестр марок отделки и позиций альбома (продолжение)

Реестр марок отделки (О ↔ позиции колерной карты) и марки позиций по видам

Марки позиций альбома по видам (продолжение)

Префикс	Что обозначает, позиции	Листы
LAN	розетки компьютерные: LAN1, LAN2	31–44
КУП	электроустановочные изделия: КУП1**, КУП2**	31–44
ЩК, ЩС**	щиты: ЩК, ЩС**	31–44
ДФ	домофон: ДФ1	31–44
АР	точки доступа Wi-Fi: АР1**	31–44
Ст В1, Ст К1, Ст К1-2 (кухня), Ст Т3	стояки (системы В1, Т3, К1): Ст В1-1, Ст В1-2, Ст В1-3, Ст К1-1, Ст К1-2 (кухня), Ст К1-3, Ст Т3-1, Ст Т3-2, Ст Т3-3	49–53
О	марки отделки (реестр альбома): О1–О26	2–6, 100–149
К, КМ	позиции колерной карты: К1–К19, КМ1–КМ6	73–76
РО	радиаторы отопления: РО-1–РО-11	45–48

Примечания

1. Марка отделки О — одна на весь альбом: одна и та же отделка (материал, изделие, цвет, формат) на всех листах имеет одну марку; на развёртках и планах стоят марки этого реестра.
2. Столбец «Колер. карта» — позиции колерной карты (лист 73): К — окраска по коду цвета, КМ — материал без кода цвета; «Помещения» — номера по экспликации; количества — по ведомости отделки помещений (лист 70).
3. Марки позиций: один префикс — один вид позиций на весь альбом (двери Д, окна ОК, мебель М, сантехприборы П, декор ДК, текстиль Т, колерная карта К и КМ, радиаторы РО, розетки Р, выключатели S, светильники Св; стояки — «Ст» и система, например «Ст К1-1»). Совпадение префиксов у разных видов — замечание к исходным данным, при выпуске исправляется в модели.

Допущения и предложения на листе

Основа листа: размеры и контуры этажей подобраны проектировщиком по составу помещений и площадям этажей с картинки 470 px (размеры на ней не читаются); обмер и исходный проект — задание (К-1); высоты: 1-й этаж 2800 мм, мансарда 2700 мм (горизонтальная часть) приняты; скаты кровли мансарды приняты по картинке: колено 1200 мм, уклон 45°, конёк вдоль длинной стороны; проект КР — задание (К-2); наружные стены 400 мм, перегородки 120 мм приняты (К-1); разрешённая мощность 15 кВт принята по типовым ТУ для частного дома (К-4); подрайон климата не задан — принят не северный (жилые от 2,5 м) (К-7).

Знак «**» — предложение проектировщика, заказчиком не утверждено (согласовать с заказчиком): записи в реестре нет: КУП1, КУП2 — по образцу: Добавлены выводы к вентиляторам: ЭВ4 (ВР1, ванная) и ЭВ5 (ВР3, санузел 2) — группа 3, высота 2389 мм, включение с основным светом, таймер выбега в вентиляторе; и коробки уравнивания потенциалов КУП1 (ванная) и КУП2 (санузел 2) — высота 300 мм, у входа, вне зон 0–2, проводник от шины РЕ щита ЩК, сече; ЩС — щит слаботочный: место и состав; АР1 — точка доступа Wi-Fi: число и места; плинтус пом. 1, 2, 4–14, 16, 17, фартук пом. 1, акцент пом. 5 — артикул изделия не выбран: позиция описана характеристиками («аналог по характеристикам»), артикул выбирается при закупке; пол пом. 10 — покрытие пола гаража — предложение исполнителя: выдерживает шины, масло и антигололёдные реагенты, без швов.

См. лист открытых вопросов (лист 7, записи К-1, К-2, К-4, К-7).

Изм.	Кол.уч	Лист	№ док.	Подп.	Дата
Разраб.		Кырлан А.С.			21.10.26
Пров.					
ГИП					
Н. контр.					
Утв.					

ГД-2026-010-АИ

Дом 331 м²

Общая площадь 270,67* м² · * размеры приняты, не замерены (реестр — л. 7, К-1)

Дизайн-проект интерьера

Стадия	Лист	Листов
РП	101	159

Реестр марок отделки и позиций альбома (продолжение)

М б/м

Кырлан Александр Сергеевич

Схема расположения развёрток и узлов

План квартиры: марки развёрток по помещениям, выноски узлов, ведомость «марка → лист»

ПРЕДВАРИТЕЛЬНО · не для производства работ · открыто пунктов: 6 (реестр — л. 7)

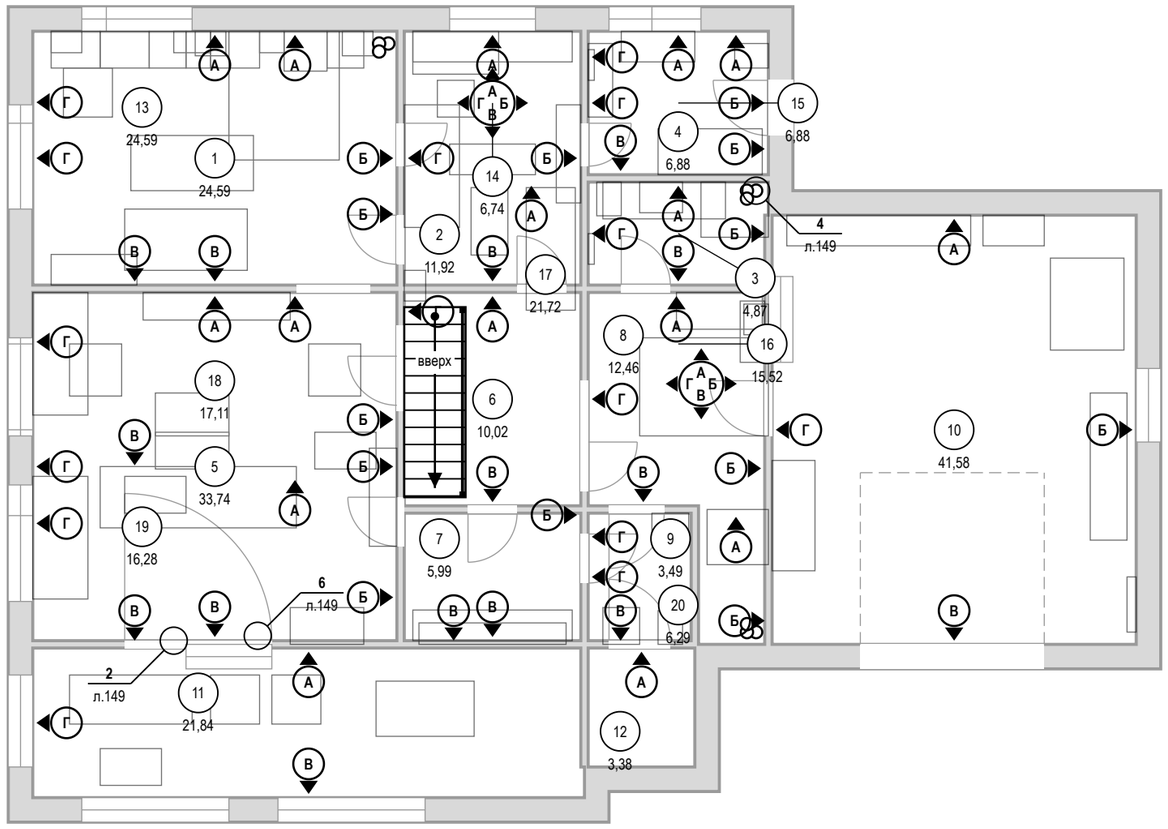

Допущения и предложения на листе

Основа листа: размеры и контуры этажей подобраны проектировщиком по составу помещений и площадям этажей с картинки 470 px (размеры на ней не читаются); обмер и исходный проект — задание (К-1); высоты: 1-й этаж 2800 мм, мансарда 2700 мм (горизонтальная часть) приняты; скаты кровли мансарды приняты по картинке: колено 1200 мм, уклон 45°, конёк вдоль длинной стороны; проект КР — задание (К-2); наружные стены 400 мм, перегородки 120 мм приняты (К-1); разрешённая мощность 15 кВт принята по типовым ТУ для частного дома (К-4); подрайон климата не задан — принят не северный (жилые от 2,5 м) (К-7).
См. лист открытых вопросов (лист 7, записи К-1, К-2, К-4, К-7).

Развёртки и узлы: марка → лист

Марка	Помещение / узел	Лист
А	Кухня-столовая (пом. 1)	103
Б, В	Кухня-столовая (пом. 1)	104
Г	Кухня-столовая (пом. 1)	105
А, Б	Кабинет-гостевая (пом. 2)	106
В, Г	Кабинет-гостевая (пом. 2)	107
А	Санузел 1 этажа (пом. 3)	108
Б, В	Санузел 1 этажа (пом. 3)	109
Г	Санузел 1 этажа (пом. 3)	110
А, Б, Г	Котельная (пом. 4)	111
А	Гостиная (пом. 5)	112
Б	Гостиная (пом. 5)	113
В	Гостиная (пом. 5)	114
Г	Гостиная (пом. 5)	115
А, В	Холл с лестницей (пом. 6)	116
В	Кладовая (пом. 7)	117
А, Б	Прихожая (пом. 8)	118
В, Г	Прихожая (пом. 8)	119
Г	Тамбур (пом. 9)	120
А	Гараж (пом. 10)	121
Б	Гараж (пом. 10)	122
В	Гараж (пом. 10)	123
Г	Гараж (пом. 10)	124
А	Веранда (пом. 11)	125
В	Веранда (пом. 11)	126
Г	Веранда (пом. 11)	127
А	Крыльцо (пом. 12)	128
А, Б	Спальня мастер (пом. 13)	129
В, Г	Спальня мастер (пом. 13)	130
А, Б, В	Гардеробная мастер (пом. 14)	131
Г	Гардеробная мастер (пом. 14)	132
А	Санузел мастер (пом. 15)	133
Б	Санузел мастер (пом. 15)	134
В	Санузел мастер (пом. 15)	135
…	ещё 19: см. ведомость рабочих чертежей, лист 2	

Условные обозначения

- (А) — марка развёртки: буква стены, стрелка — взгляд
- выноска узла: над полкой — узел, под полкой — лист
- (1) — номер помещения, площадь м²

1000 мм · печать 1:1

Примечания

1. Развёртки — вид на стену изнутри помещения; буквы стен — одна система на весь альбом (как на листах выводов, плитки и отделки).
2. Стены без электроточек, мебели, декора и акцентной отделки развёрток не имеют: их отделка — по ведомости отделки помещений.
3. Узлы — на листе узлов; места применения — по выноскам этого листа и ведомости «марка → лист».

Изм.	Кол.уч	Лист	№ док.	Подп.	Дата
Разраб.		Кырлан А.С.			21.10.26
Пров.					
ГИП					
Н. контр.					
Утв.					

ГД-2026-010-АИ

Дом 331 м²

Общая площадь 270,67* м² · * размеры приняты, не замерены (реестр — л. 7, К-1)

Дизайн-проект интерьера

Стадия	Лист	Листов
РП	102	159

Схема расположения развёрток и узлов

М 1:100

Кырлан Александр Сергеевич

выпуск 18.10.2026 № 9365d64cec · стр. 108 из 197

Развёртка стены А. Кухня-столовая (пом. 1), кухонный фронт

Кухня-столовая (пом. 1) · вид изнутри помещения · размеры в мм, отметки в м

ПРЕДВАРИТЕЛЬНО · не для производства работ · открыто пунктов: 6 (реестр — л. 7)

Развёртка стены А

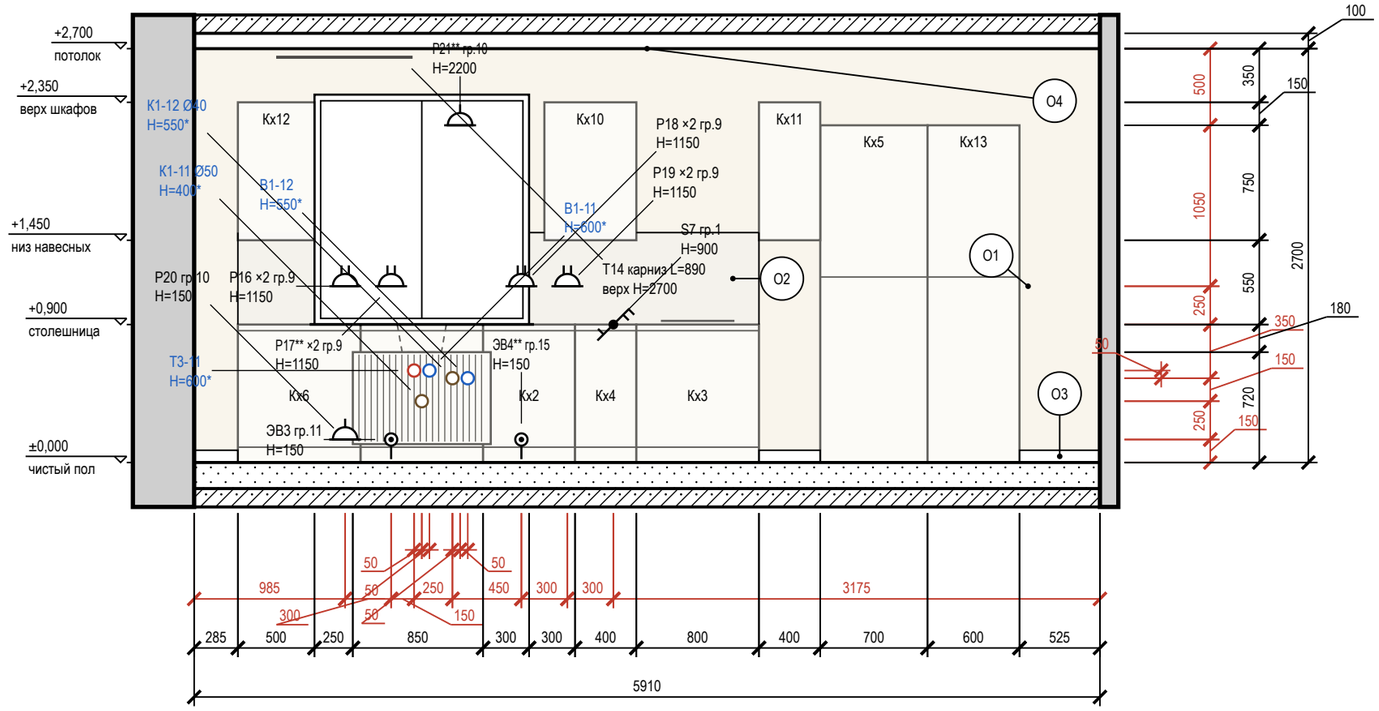

Условные обозначения

- розетка с заземляющим контактом; у знака — марка, ×N постов в рамке, гр. — группа щита, H — высота оси, мм
- вывод кабеля для подключения прибора (без розетки), марка ЭВ
- выключатель одноклавишный
- выключатель двухклавишный (флажков — по числу клавиш)
- выключатель с проходной или перекрёстной клавишей (обратный флажок); тип клавиши — в подписи
- вывод В1 (код — в ведомости привязок)
- вывод Т3 (код — в ведомости привязок)
- вывод К1 (код — в ведомости привязок)
- привязки точек и выводов от угла и от пола, мм
- мебель и приборы — фасад по расстановке (условно)
- карниз (шина) и шторы в собранном виде: марка Т, длина L, верх H
- окно: проём, рама, подоконник
- радиатор отопления; марка — по плану отопления
- стены и перекрытия в сечении
- плитка: сетка швов по формату, ▲ — ось старта
- окраска: тон — цвет по коду производителя (условно)
- О1 — марка отделки по реестру отделки альбома
- А — марка развёртки: буква стены, стрелка — взгляд

Схема развёрток (М 1:100)

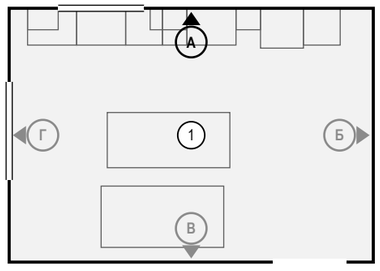

Ведомость отделки (на листе)

Марка	Поверхность	Материал, изделие	Цвет, код	Кол.
О1	стены	окраска, Tikkurila Luja 7, шелковисто-матовая, подготовка К3	NCS S 0804-Y30R «S 0804-Y30R»	11,8 м²
О2	фартук	керамогранит, аналог: керамогранит матовый, тон F497, затирка CG2WA	#F1F1EC «тон Paper F497»	1,2 м²
О3	плинтус	плинтус МДФ, h 80 мм, аналог: плинтус МДФ под окраску 80×16 мм, полуглянцевая	NCS S 0804-Y30R «S 0804-Y30R»	1,2 м
О4	потолок	окраска, Tikkurila Luja 7, матовая, подготовка Q3	NCS S 0804-Y30R «S 0804-Y30R»	24,6 м²

Допущения и предложения на листе

Основа листа: размеры и контуры этажей подобраны проектировщиком по составу помещений и площадям этажей с картинки 470 px (размеры на ней не читаются); обмер и исходный проект — задание (К-1); высоты: 1-й этаж 2800 мм, мансарда 2700 мм (горизонтальная часть) приняты; скаты кровли мансарды приняты по картинке: колено 1200 мм, уклон 45°, конёк вдоль длинной стороны; проект КР — задание (К-2); наружные стены 400 мм, перегородки 120 мм приняты (К-1); разрешённая мощность 15 кВт принята по типовым ТУ для частного дома (К-4); подрайон климата не задан — принят не северный (жилые от 2,5 м) (К-7).
Знак «**» — предложение проектировщика, заказчиком не утверждено (согласовать с заказчиком): записи в реестре нет: Р21 — высота 2200 мм выше нормы 1 м (ПУЭ 6.6.30) по назначению: питание вытяжки М25, розетка в модуле за съёмной панелью; ЭВ4 — по образцу: Добавлены выводы к вентиляторам: ЭВ4 (ВР1, ванная) и ЭВ5 (ВР3, санузел 2) — группа 3, высота 2389 мм, включение с основным светом, таймер выбега в вентиляторе; и коробки уравнивания потенциалов КУП1 (ванная) и КУП2 (санузел 2) — высота 300 мм, у входа, вне зон 0–2, проводник от шины PE щита ЩК, сече; Р17 — высота 1700 мм выше нормы 1 м (ПУЭ 6.6.30) по назначению: питание слаботочного щита ЩС, рядом со щитом на его высоте.
См. лист открытых вопросов (лист 7, записи К-1, К-2, К-4, К-7).

Примечания

1. Развёртки — вид на стену изнутри помещения, по часовой стрелке; расположение — на схеме листа и на листе 102; размеры — в мм по чистовым поверхностям; отметки — в м от ±0,000; высоты H — от чистого пола помещения до оси изделия, у декора — до центра.
2. Красные цепочки — привязки электроточек и выводов: по горизонтали от угла чистовых стен, по вертикали от чистого пола, до оси изделия; звенья короче 3 мм на листе вынесены во второй ярус (ближняя к стене цепочка).
3. У знака электроточки: марка (Р — розетка, S — выключатель, Св — светильник, ЭВ — вывод кабеля), ×N — число постов в рамке, гр. — группа щита, H — высота оси от чистого пола, мм; группы по клавишам выключателя — на листе выключателей.
4. Схема мебели, приборов и декора не является технической документацией для производства мебели; габариты — по паспортам изделий.
5. Выводы ВК — коды и высоты по листу выводов сантехники; * — высота принята по типовой практике монтажа, окончательно — по паспорту прибора.
6. Карнизы (шины) — по ведомости текстиля декоратора; длина L и верх H — по развёртке, крепление — до окраски потолка.
7. Выводы кухонной техники — по утверждённому проекту кухни: привязки выводов даются от осей модулей гарнитура.
8. Потолок на развёртках — по нижнему уровню У2; другие уровни потолка помещения: У3 +2,600, У1 +2,700.

1000 мм · печать 1:1

Изм.	Кол.уч	Лист	№ док.	Подп.	Дата
Разраб.		Кырлан А.С.			21.10.26
Пров.					
ГИП					
Н. контр.					
Утв.					

ГД-2026-010-АИ

Дом 331 м²

Общая площадь 270,67* м² · * размеры приняты, не замерены (реестр — л. 7, К-1)

Дизайн-проект интерьера

Стадия	Лист	Листов
РП	103	159

Развёртка стены А. Кухня-столовая (пом. 1), кухонный фронт

М 1:40

Кырлан Александр Сергеевич

Развёртки стен Б, В. Кухня-столовая (пом. 1)

Кухня-столовая (пом. 1) · вид изнутри помещения · размеры в мм, отметки в м

ПРЕДВАРИТЕЛЬНО · не для производства работ · открыто пунктов: 6 (реестр — л. 7)

Развёртка стены Б

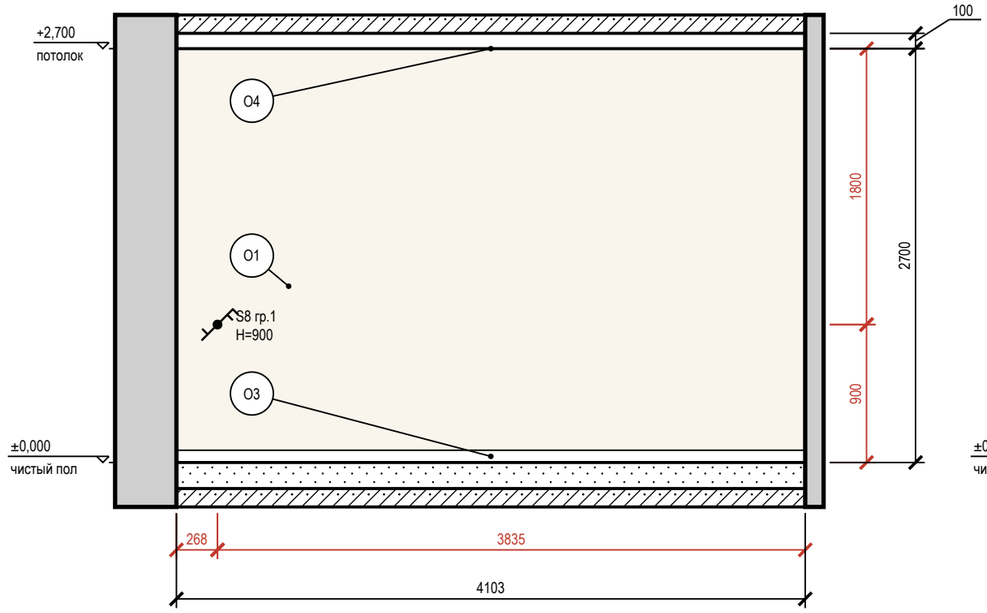

Развёртка стены В

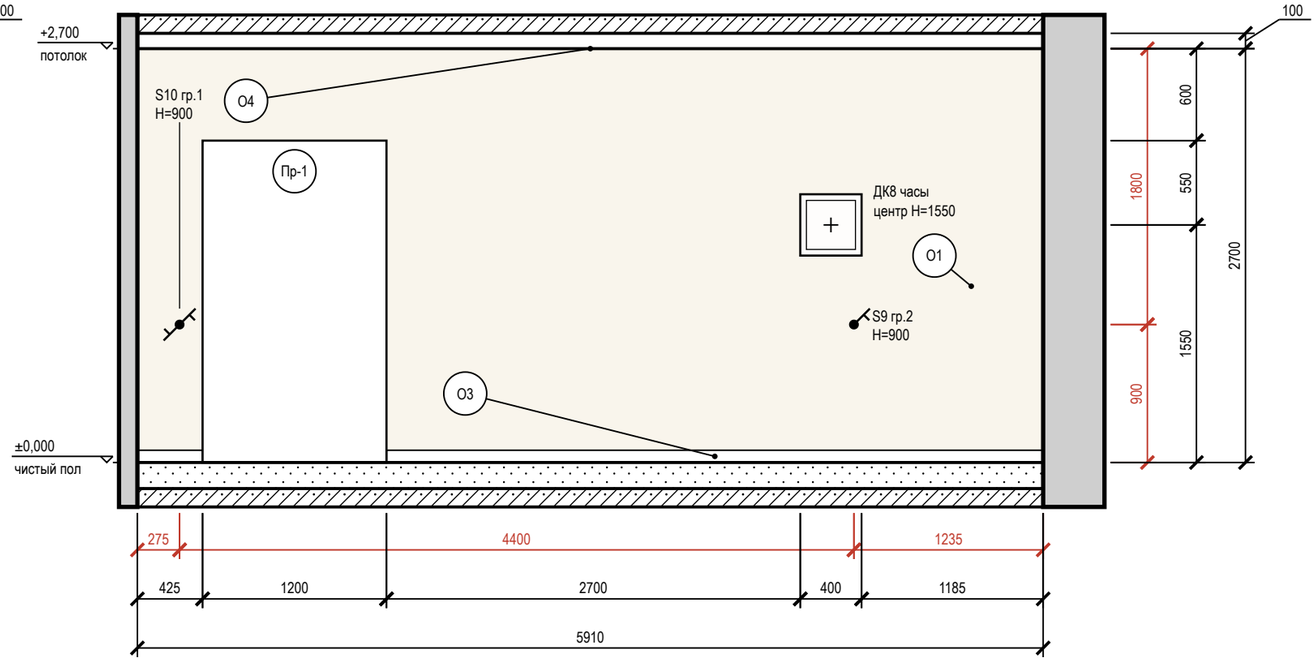

Схема развёрток (М 1:100)

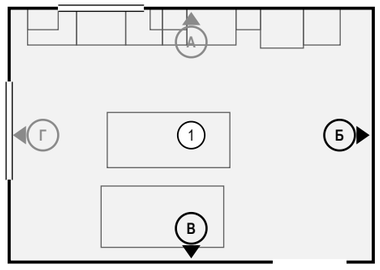

Условные обозначения

- выключатель одноклавишный
- выключатель двухклавишный (флажков — по числу клавиш)
- выключатель с проходной или перекрёстной клавишей (обратный флажок); тип клавиши — в подписи
- привязки точек и выводов от угла и от пола, мм
- мебель и приборы — фасад по расстановке (условно)
- картина (декор): марка Д, крест — центр, Н — высота центра, мм
- дверной проём; марка двери — в кружке
- стены и перекрытия в сечении
- окраска: тон — цвет по коду производителя (условно)
- О1 — марка отделки по реестру отделки альбома
- А — марка развёртки: буква стены, стрелка — взгляд

Ведомость отделки (на листе)

Марка	Поверхность	Материал, изделие	Цвет, код	Кол.
О1	стены	окраска, Tikkurila Luja 7, шелковисто-матовая, подготовка К3	NCS S 0804-Y30R «S 0804-Y30R»	24,5 м²
О3	плинтус	плинтус МДФ, h 80 мм, аналог: плинтус МДФ под окраску 80×16 мм, полуглянцевая	NCS S 0804-Y30R «S 0804-Y30R»	8,8 м
О4	потолок	окраска, Tikkurila Luja 7, матовая, подготовка Q3	NCS S 0804-Y30R «S 0804-Y30R»	24,6 м²

Допущения и предложения на листе

Основа листа: размеры и контуры этажей подобраны проектировщиком по составу помещений и площадям этажей с картинки 470 px (размеры на ней не читаются); обмер и исходный проект — задание (К-1); высоты: 1-й этаж 2800 мм, мансарда 2700 мм (горизонтальная часть) приняты; скаты кровли мансарды приняты по картинке: колено 1200 мм, уклон 45°, конёк вдоль длинной стороны; проект КР — задание (К-2); наружные стены 400 мм, перегородки 120 мм приняты (К-1); разрешённая мощность 15 кВт принята по типовым ТУ для частного дома (К-4); подрайон климата не задан — принят не северный (жилые от 2,5 м) (К-7).

См. лист открытых вопросов (лист 7, записи К-1, К-2, К-4, К-7).

Примечания

1. Развёртки — вид на стену изнутри помещения, по часовой стрелке; расположение — на схеме листа и на листе 102; размеры — в мм по чистовым поверхностям; отметки — в м от ±0,000; высоты Н — от чистого пола помещения до оси изделия, у декора — до центра.
2. Красные цепочки — привязки электроточек и выводов: по горизонтали от угла чистовых стен, по вертикали от чистого пола, до оси изделия; звенья короче 3 мм на листе вынесены во второй ярус (ближняя к стене цепочка).
3. У знака электроточки: марка (Р — розетка, S — выключатель, Св — светильник, ЭВ — вывод кабеля), ×N — число постов в рамке, гр. — группа щита, Н — высота оси от чистого пола, мм; группы по клавишам выключателя — на листе выключателей.
4. Схема мебели, приборов и декора не является технической документацией для производства мебели; габариты — по паспортам изделий.
5. Картины и зеркала крепить к основанию по паспорту изделия (закладные и анкеры — в перечне скрытых работ); крест — ось центра предмета.
6. Потолок на развёртках — по нижнему уровню У2; другие уровни потолка помещения: У3 +2,600, У1 +2,700.

1000 мм · печать 1:1

Изм.	Кол.уч	Лист	№ док.	Подп.	Дата
Разраб.		Кырлан А.С.			21.10.26
Пров.					
ГИП					
Н. контр.					
Утв.					

ГД-2026-010-АИ

Дом 331 м²

Общая площадь 270,67* м² · * размеры приняты, не замерены (реестр — л. 7, К-1)

Дизайн-проект интерьера

Стадия	Лист	Листов
РП	104	159

Развёртки стен Б, В. Кухня-столовая (пом. 1)

М 1:40

Кырлан Александр Сергеевич

выпуск 18.10.2026 № 9365d64cec · стр. 110 из 197

Развёртка стены Г. Кухня-столовая (пом. 1)

Кухня-столовая (пом. 1) · вид изнутри помещения · размеры в мм, отметки в м

ПРЕДВАРИТЕЛЬНО · не для производства работ · открыто пунктов: 6 (реестр — л. 7)

Развёртка стены Г

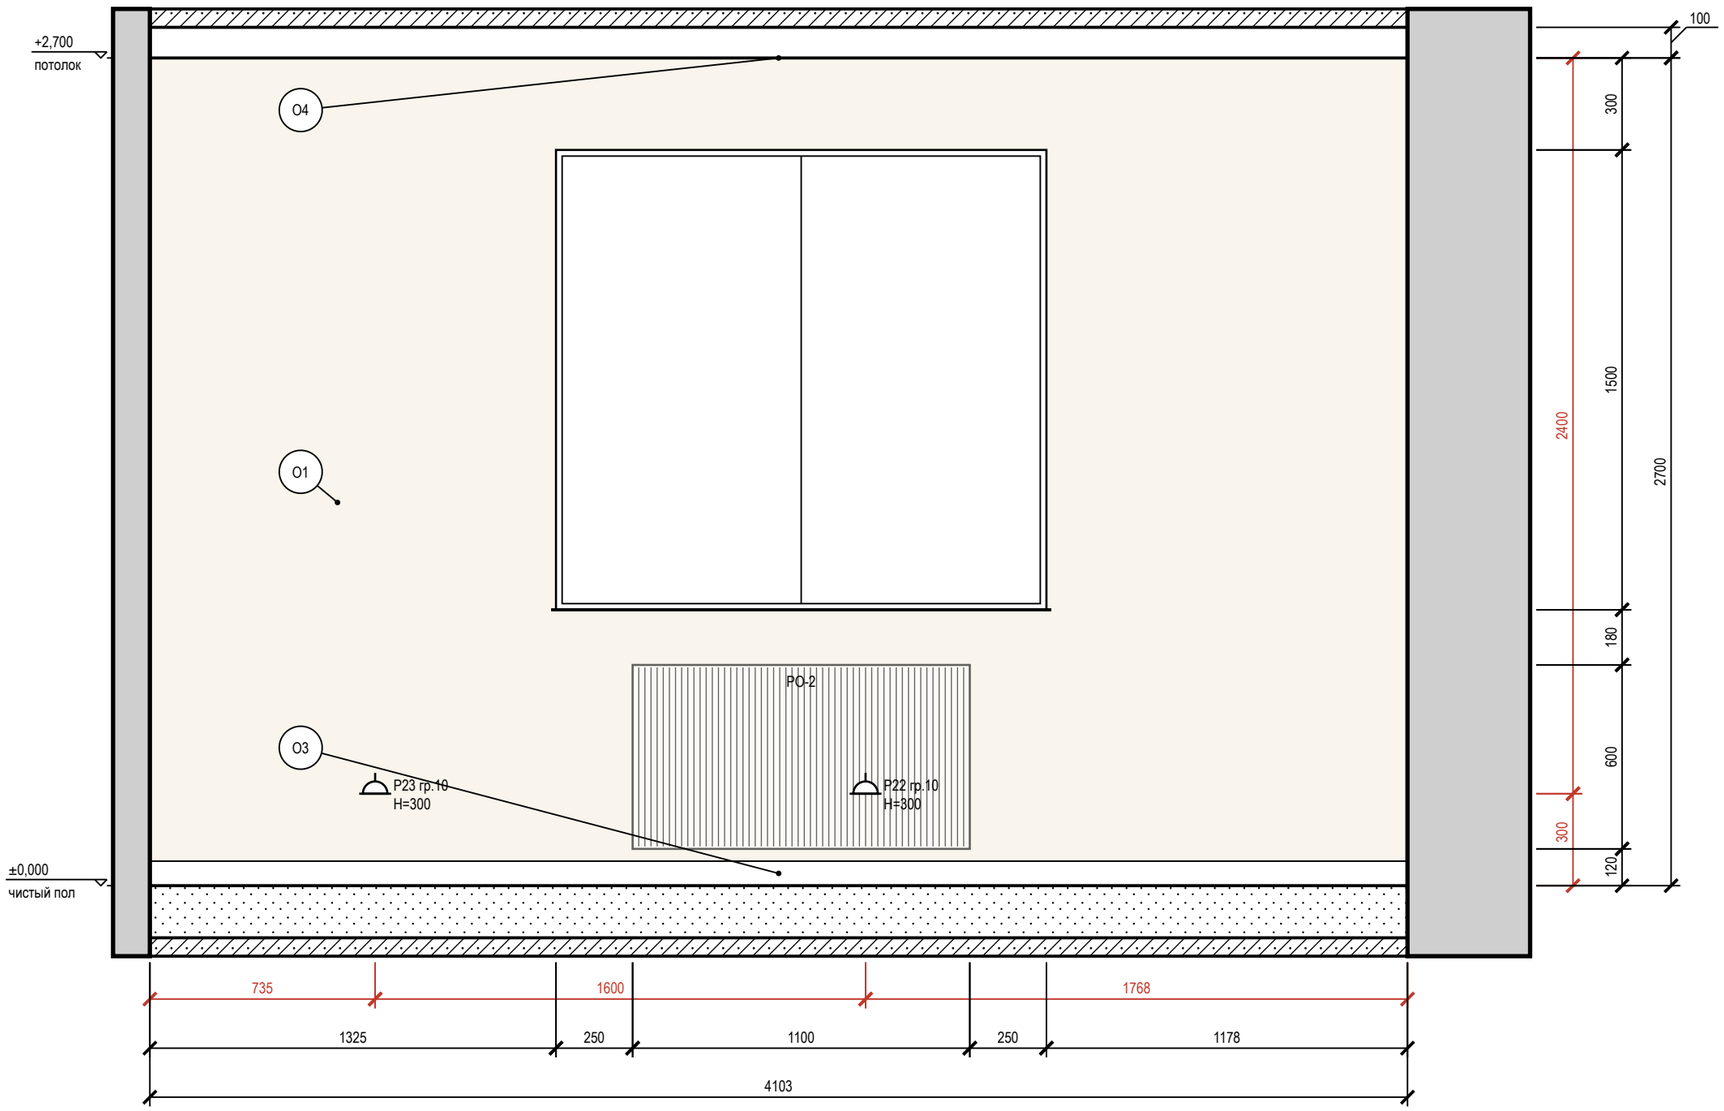

Схема развёрток (М 1:100)

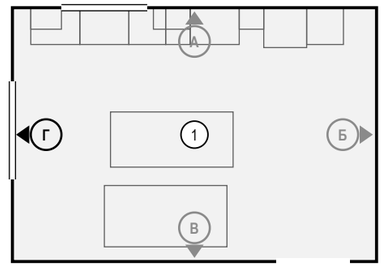

Условные обозначения

- розетка с заземляющим контактом; у знака — марка, ×N постов в рамке, гр. — группа щита, Н — высота оси, мм
- привязки точек и выводов от угла и от пола, мм
- мебель и приборы — фасад по расстановке (условно)
- окно: проём, рама, подоконник
- радиатор отопления; марка — по плану отопления
- стены и перекрытия в сечении
- окраска: тон — цвет по коду производителя (условно)
- О1 — марка отделки по реестру отделки альбома
- А — марка развёртки: буква стены, стрелка — взгляд

Допущения и предложения на листе

Основа листа: размеры и контуры этажей подобраны проектировщиком по составу помещений и площадям этажей с картинки 470 px (размеры на ней не читаются); обмер и исходный проект — задание (К-1); высоты: 1-й этаж 2800 мм, мансарда 2700 мм (горизонтальная часть) приняты; скаты кровли мансарды приняты по картинке: колено 1200 мм, уклон 45°, конёк вдоль длинной стороны; проект КР — задание (К-2); наружные стены 400 мм, перегородки 120 мм приняты (К-1); разрешённая мощность 15 кВт принята по типовым ТУ для частного дома (К-4); подрайон климата не задан — принят не северный (жилые от 2,5 м) (К-7).

См. лист открытых вопросов (лист 7, записи К-1, К-2, К-4, К-7).

Примечания

1. Развёртки — вид на стену изнутри помещения, по часовой стрелке; расположение — на схеме листа и на листе 102; размеры — в мм по чистовым поверхностям; отметки — в м от ±0,000; высоты Н — от чистого пола помещения до оси изделия, у декора — до центра.
2. Красные цепочки — привязки электроточек и выводов: по горизонтали от угла чистовых стен, по вертикали от чистого пола, до оси изделия; звенья короче 3 мм на листе вынесены во второй ярус (ближняя к стене цепочка).
3. У знака электроточки: марка (Р — розетка, S — выключатель, Св — светильник, ЭВ — вывод кабеля), ×N — число постов в рамке, гр. — группа щита, Н — высота оси от чистого пола, мм; группы по клавишам выключателя — на листе выключателей.
4. Схема мебели, приборов и декора не является технической документацией для производства мебели; габариты — по паспортам изделий.
5. Потолок на развёртках — по нижнему уровню У2; другие уровни потолка помещения: У3 +2,600, У1 +2,700.

1000 мм · печать 1:1

Изм.	Кол.уч	Лист	№ док.	Подп.	Дата
Разраб.		Кырлан А.С.			21.10.26
Пров.					
ГИП					
Н. контр.					
Утв.					

ГД-2026-010-АИ

Дом 331 м²

Общая площадь 270,67* м² · * размеры приняты, не замерены (реестр — л. 7, К-1)

Дизайн-проект интерьера

Стадия	Лист	Листов
РП	105	159

Развёртка стены Г. Кухня-столовая (пом. 1)

М 1:20

Кырлан Александр Сергеевич

выпуск 18.10.2026 № 9365d64cec · стр. 111 из 197

Развёртки стен А, Б. Кабинет-гостевая (пом. 2)

Кабинет-гостевая (пом. 2) · вид изнутри помещения · размеры в мм, отметки в м

ПРЕДВАРИТЕЛЬНО · не для производства работ · открыто пунктов: 6 (реестр — л. 7)

Развёртка стены А

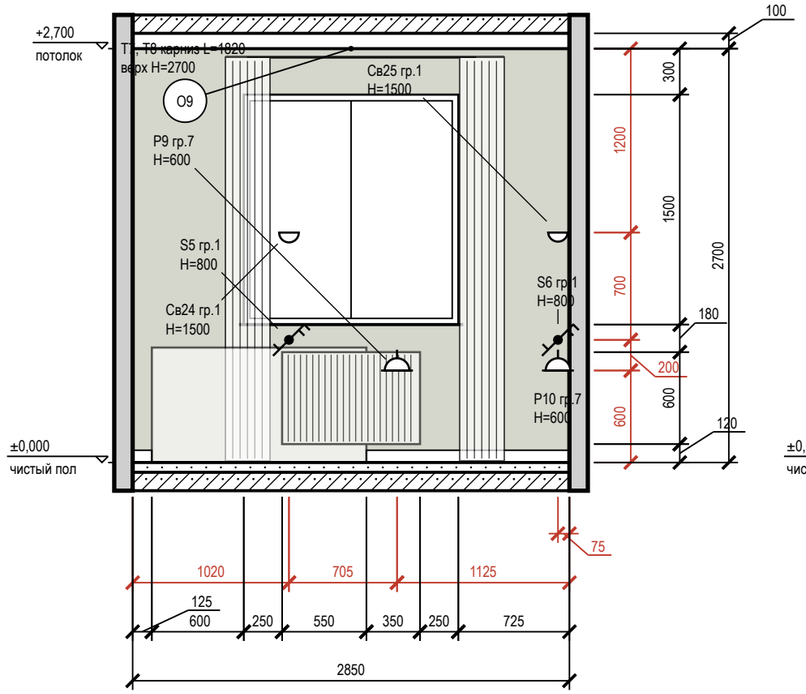

Развёртка стены Б

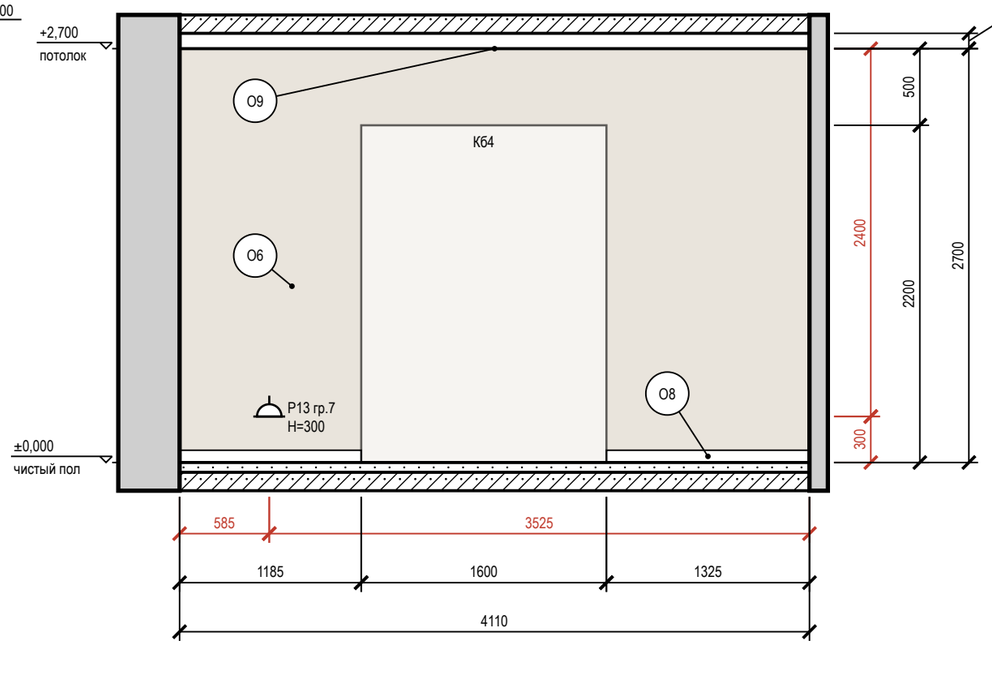

Условные обозначения

- розетка с заземляющим контактом; у знака — марка, ×N постов в рамке, гр. — группа щита, H — высота оси, мм
- выключатель одноклавишный
- выключатель двухклавишный (флажков — по числу клавиш)
- выключатель с проходной или перекрёстной клавишей (обратный флажок); тип клавиши — в подписи
- светильник настенный (бра), H — высота оси
- привязки точек и выводов от угла и от пола, мм
- мебель и приборы — фасад по расстановке (условно)
- карниз (шина) и шторы в собранном виде: марка T, длина L, верх H
- окно: проём, рама, подоконник
- радиатор отопления; марка — по плану отопления
- стены и перекрытия в сечении
- окраска: тон — цвет по коду производителя (условно)
- О1 — марка отделки по реестру отделки альбома
- А — марка развёртки: буква стены, стрелка — взгляд

Схема развёрток (М 1:100)

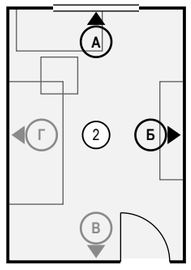

Ведомость отделки (на листе)

Марка	Поверхность	Материал, изделие	Цвет, код	Кол.
О6	стены	окраска, Farrow & Ball Modern Emulsion, матовая, подготовка Q3	Farrow & Ball No. 226 «Joa's White»	11,1 м²
О7	акцентная стена	окраска, Farrow & Ball Modern Emulsion, матовая, подготовка Q3	Farrow & Ball No. 298 «Bancha»	5,6 м²
О8	плинтус	плинтус МДФ, h 80 мм, аналог: плинтус МДФ под покраску 80×16	Farrow & Ball No. 226 «Joa's White»	4 м
О9	потолок	окраска, Tikkurila Anti-Reflex 2, глубокоматовая, подготовка Q3	Little Greene No. 105 «Slaked Lime»	11,9 м²

Допущения и предложения на листе

Основа листа: размеры и контуры этажей подобраны проектировщиком по составу помещений и площадям этажей с картинки 470 px (размеры на ней не читаются); обмер и исходный проект — задание (К-1); высоты: 1-й этаж 2800 мм, мансарда 2700 мм (горизонтальная часть) приняты; скаты кровли мансарды приняты по картинке: колено 1200 мм, уклон 45°, конёк вдоль длинной стороны; проект КР — задание (К-2); наружные стены 400 мм, перегородки 120 мм приняты (К-1); разрешённая мощность 15 кВт принята по типовым ТУ для частного дома (К-4); подрайон климата не задан — принят не северный (жилые от 2,5 м) (К-7).

См. лист открытых вопросов (лист 7, записи К-1, К-2, К-4, К-7).

Примечания

1. Развёртки — вид на стену изнутри помещения, по часовой стрелке; расположение — на схеме листа и на листе 102; размеры — в мм по чистовым поверхностям; отметки — в м от ±0,000; высоты H — от чистого пола помещения до оси изделия, у декора — до центра.
2. Красные цепочки — привязки электроточек и выводов: по горизонтали от угла чистовых стен, по вертикали от чистого пола, до оси изделия; звенья короче 3 мм на листе вынесены во второй ярус (ближняя к стене цепочка).
3. У знака электроточки: марка (Р — розетка, S — выключатель, Св — светильник, ЭВ — вывод кабеля), ×N — число постов в рамке, гр. — группа щита, H — высота оси от чистого пола, мм; группы по клавишам выключателя — на листе выключателей.
4. Схема мебели, приборов и декора не является технической документацией для производства мебели; габариты — по паспортам изделий.
5. Карнизы (шины) — по ведомости текстиля декоратора; длина L и верх H — по развёртке, крепление — до окраски потолка.
6. Потолок на развёртках — по нижнему уровню У2; другие уровни потолка помещения: У1 +2,700.

1000 мм · печать 1:1

Изм.	Кол.уч	Лист	№ док.	Подп.	Дата
Разраб.		Кырлан А.С.			21.10.26
Пров.					
ГИП					
Н. контр.					
Утв.					

ГД-2026-010-АИ

Дом 331 м²

Общая площадь 270,67* м² · * размеры приняты, не замерены (реестр — л. 7, К-1)

Дизайн-проект интерьера

Стадия	Лист	Листов
РП	106	159

Развёртки стен А, Б. Кабинет-гостевая (пом. 2)

М 1:40

Кырлан Александр Сергеевич

выпуск 18.10.2026 № 9365d64cec · стр. 112 из 197

Развёртки стен В, Г. Кабинет-гостевая (пом. 2)

Кабинет-гостевая (пом. 2) · вид изнутри помещения · размеры в мм, отметки в м

ПРЕДВАРИТЕЛЬНО · не для производства работ · открыто пунктов: 6 (реестр — л. 7)

Развёртка стены В

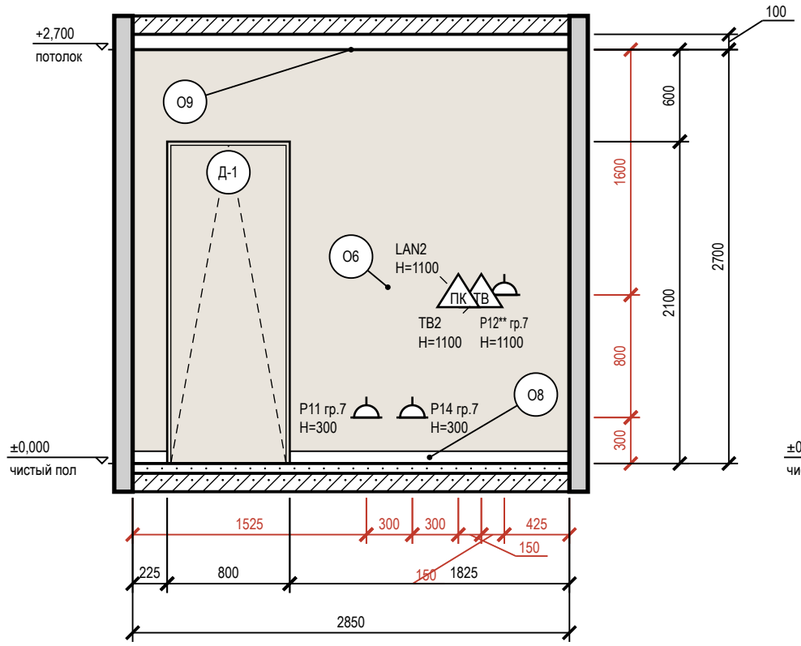

Развёртка стены Г

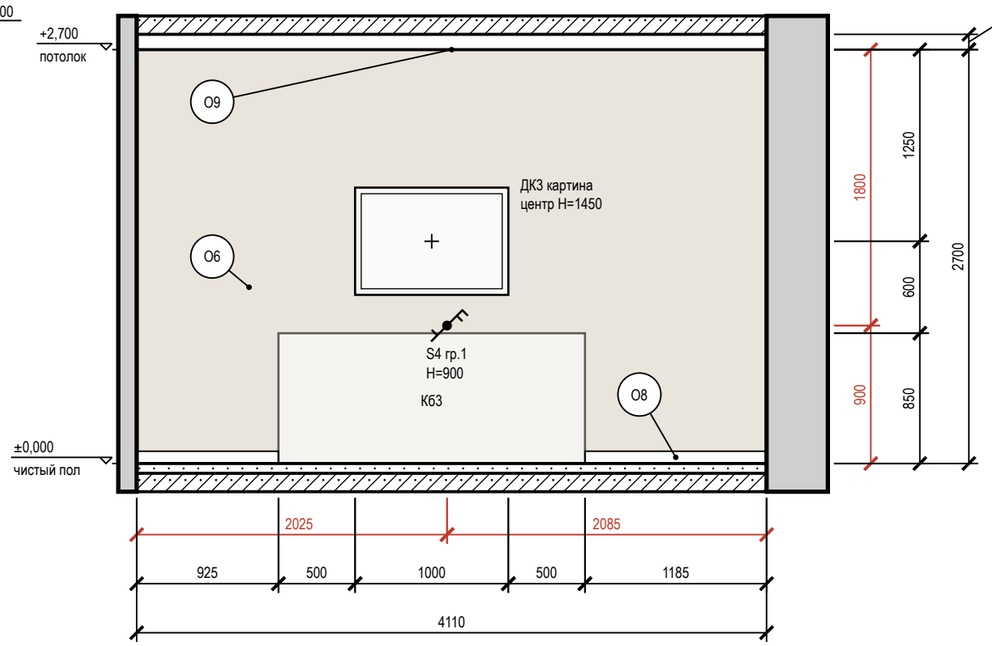

Условные обозначения

- розетка с заземляющим контактом; у знака — марка, ×N постов в рамке, гр. — группа щита, H — высота оси, мм
- выключатель одноклавишный
- выключатель двухклавишный (флажков — по числу клавиш)
- выключатель с проходной или перекрёстной клавишей (обратный флажок); тип клавиши — в подписи
- ПК — розетка компьютерная RJ45
- ТВ — розетка телевизионная
- привязки точек и выводов от угла и от пола, мм
- мебель и приборы — фасад по расстановке (условно)
- картина (декор): марка Д, крест — центр, H — высота центра, мм
- дверь скрытого монтажа: полотно в плоскости стены (узел — на листе узлов)
- стены и перекрытия в сечении
- окраска: тон — цвет по коду производителя (условно)
- О1 — марка отделки по реестру отделки альбома
- А — марка развёртки: буква стены, стрелка — взгляд

Схема развёрток (М 1:100)

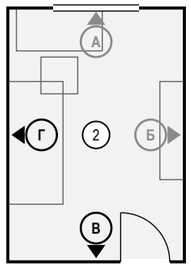

Ведомость отделки (на листе)

Марка	Поверхность	Материал, изделие	Цвет, код	Кол.
О6	стены	окраска, Farrow & Ball Modern Emulsion, матовая, подготовка Q3	Farrow & Ball No. 226 «Joa's White»	17,1 м²
О8	плинтус	плинтус МДФ, h 80 мм, аналог: плинтус МДФ под покраску 80×16	Farrow & Ball No. 226 «Joa's White»	4,2 м
О9	потолок	окраска, Tikkurila Anti-Reflex 2, глубокоматовая, подготовка Q3	Little Greene No. 105 «Slaked Lime»	11,9 м²

Допущения и предложения на листе

Основа листа: размеры и контуры этажей подобраны проектировщиком по составу помещений и площадям этажей с картинки 470 px (размеры на ней не читаются); обмер и исходный проект — задание (К-1); высоты: 1-й этаж 2800 мм, мансарда 2700 мм (горизонтальная часть) приняты; скаты кровли мансарды приняты по картинке: колено 1200 мм, уклон 45°, конёк вдоль длинной стороны; проект КР — задание (К-2); наружные стены 400 мм, перегородки 120 мм приняты (К-1); разрешённая мощность 15 кВт принята по типовым ТУ для частного дома (К-4); подрайон климата не задан — принят не северный (жилые от 2,5 м) (К-7).

Знак «**» — предложение проектировщика, заказчиком не утверждено (согласовать с заказчиком): записи в реестре нет: Р12 — высота 1100 мм выше нормы 1 м (ПУЭ 6.6.30) по назначению: питание ТВ над комодом, в одной зоне с выводами ТВ2 и LAN2.

См. лист открытых вопросов (лист 7, записи К-1, К-2, К-4, К-7).

Примечания

1. Развёртки — вид на стену изнутри помещения, по часовой стрелке; расположение — на схеме листа и на листе 102; размеры — в мм по чистовым поверхностям; отметки — в м от ±0,000; высоты H — от чистого пола помещения до оси изделия, у декора — до центра.
2. Красные цепочки — привязки электроточек и выводов: по горизонтали от угла чистовых стен, по вертикали от чистого пола, до оси изделия; звенья короче 3 мм на листе вынесены во второй ярус (ближняя к стене цепочка).
3. У знака электроточки: марка (Р — розетка, S — выключатель, Св — светильник, ЭВ — вывод кабеля), ×N — число постов в рамке, гр. — группа щита, H — высота оси от чистого пола, мм; группы по клавишам выключателя — на листе выключателей.
4. Схема мебели, приборов и декора не является технической документацией для производства мебели; габариты — по паспортам изделий.
5. Картины и зеркала крепить к основанию по паспорту изделия (закладные и анкеры — в перечне скрытых работ); крест — ось центра предмета.
6. Двери скрытого монтажа — полотно в плоскости стены, отделка стены по полотну, плинтус прерывается у короба (узел — на листе узлов).
7. Потолок на развёртках — по нижнему уровню У2; другие уровни потолка помещения: У1 +2,700.

1000 мм · печать 1:1

Изм.	Кол.уч	Лист	№ док.	Подп.	Дата
Разраб.		Кырлан А.С.			21.10.26
Пров.					
ГИП					
Н. контр.					
Утв.					

ГД-2026-010-АИ

Дом 331 м²

Общая площадь 270,67* м² · * размеры приняты, не замерены (реестр — л. 7, К-1)

Дизайн-проект интерьера

Стадия	Лист	Листов
РП	107	159

Развёртки стен В, Г. Кабинет-гостевая (пом. 2)

М 1:40

Кырлан Александр Сергеевич

выпуск 18.10.2026 № 9365d64cec · стр. 113 из 197

Развёртка стены А. Санузел 1 этажа (пом. 3)

Санузел 1 этажа (пом. 3) · вид изнутри помещения · размеры в мм, отметки в м

ПРЕДВАРИТЕЛЬНО · не для производства работ · открыто пунктов: 6 (реестр — л. 7)

Развёртка стены А

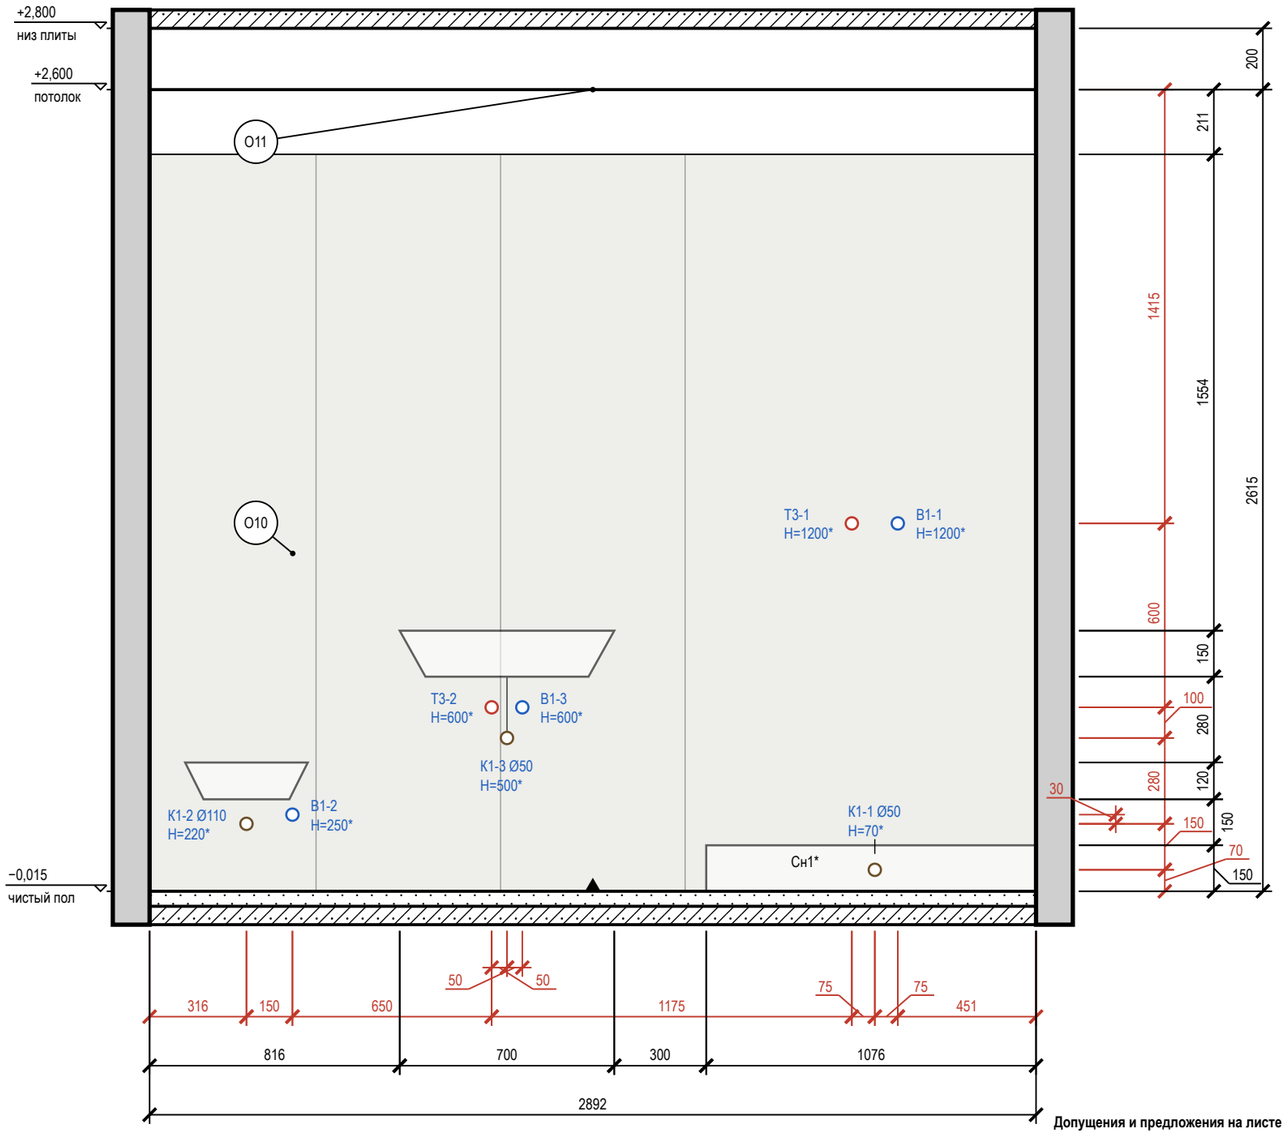

Схема развёрток (М 1:100)

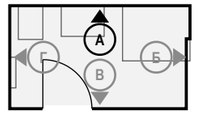

Условные обозначения

- вывод В1 (код — в ведомости привязок)
- вывод Т3 (код — в ведомости привязок)
- вывод К1 (код — в ведомости привязок)
- привязки точек и выводов от угла и от пола, мм
- мебель и приборы — фасад по расстановке (условно)
- стены и перекрытия в сечении
- плитка: сетка швов по формату, ▲ — ось старта
- О1 — марка отделки по реестру отделки альбома
- А — марка развёртки: буква стены, стрелка — взгляд

Ведомость отделки (на листе)

Марка	Поверхность	Материал, изделие	Цвет, код	Кол.
О10	стены	облицовка плиткой, Atlas Concorde Marvel Travertine, 600×1200×9 мм, А8UZ, затирка CG2WA	Atlas Concorde A8UZ «Marvel Travertine»	7 м²
О11	потолок	окраска, Tikkurila Luja 7, матовая, подготовка Q3	Little Greene No. 105 «Slaked Lime»	4,9 м²

Допущения и предложения на листе

Основа листа: размеры и контуры этажей подобраны проектировщиком по составу помещений и площадям этажей с картинки 470 px (размеры на ней не читаются); обмер и исходный проект — задание (К-1); высоты: 1-й этаж 2800 мм, мансарда 2700 мм (горизонтальная часть) приняты; скаты кровли мансарды приняты по картинке: колено 1200 мм, уклон 45°, конёк вдоль длинной стороны; проект КР — задание (К-2); наружные стены 400 мм, перегородки 120 мм приняты (К-1); разрешённая мощность 15 кВт принята по типовым ТУ для частного дома (К-4); подрайон климата не задан — принят не северный (жилые от 2,5 м) (К-7).

См. лист открытых вопросов (лист 7, записи К-1, К-2, К-4, К-7).

Примечания

1. Развёртки — вид на стену изнутри помещения, по часовой стрелке; расположение — на схеме листа и на листе 102; размеры — в мм по чистовым поверхностям; отметки — в м от ±0,000; высоты Н — от чистого пола помещения до оси изделия, у декора — до центра.
2. Красные цепочки — привязки электроточек и выводов: по горизонтали от угла чистовых стен, по вертикали от чистого пола, до оси изделия; звенья короче 3 мм на листе вынесены во второй ярус (ближняя к стене цепочка).
3. У знака электроточки: марка (Р — розетка, S — выключатель, Св — светильник, ЭВ — вывод кабеля), ×N — число постов в рамке, гр. — группа щита, Н — высота оси от чистого пола, мм; группы по клавишам выключателя — на листе выключателей.
4. Схема мебели, приборов и декора не является технической документацией для производства мебели; габариты — по паспортам изделий (* — высота не задана в проекте, показана по типовому изделию).
5. Выводы ВК — коды и высоты по листу выводов сантехники; * — высота принята по типовой практике монтажа, окончательно — по паспорту прибора.
6. Облицовка — по сетке швов 2 мм, раскладка от оси стены (треугольник у пола), целые ряды от пола; подрезки — по листу раскладки плитки.
7. Гидроизоляция в 2 слоя, заход на стены 200 мм — до облицовки, с актом скрытых работ и тестом проливом (узел — на листе узлов).

1000 мм · печать 1:1

Изм.	Кол.уч	Лист	№ док.	Подп.	Дата
Разраб.		Кырлан А.С.			21.10.26
Пров.					
ГИП					
Н. контр.					
Утв.					

ГД-2026-010-АИ

Дом 331 м²

Общая площадь 270,67* м² · * размеры приняты, не замерены (реестр — л. 7, К-1)

Дизайн-проект интерьера

Стадия	Лист	Листов
РП	108	159

Развёртка стены А. Санузел 1 этажа (пом. 3)

М 1:20

Кырлан Александр Сергеевич

выпуск 18.10.2026 № 9365d64cec · стр. 114 из 197

Развёртки стен Б, В. Санузел 1 этажа (пом. 3)

Санузел 1 этажа (пом. 3) · вид изнутри помещения · размеры в мм, отметки в м

ПРЕДВАРИТЕЛЬНО · не для производства работ · открыто пунктов: 6 (реестр — л. 7)

Развёртка стены Б

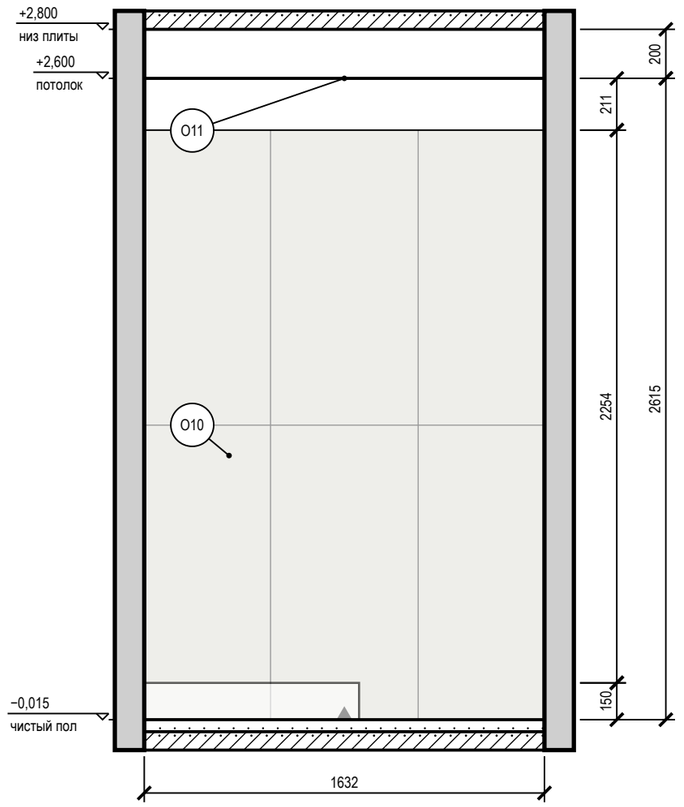

Развёртка стены В

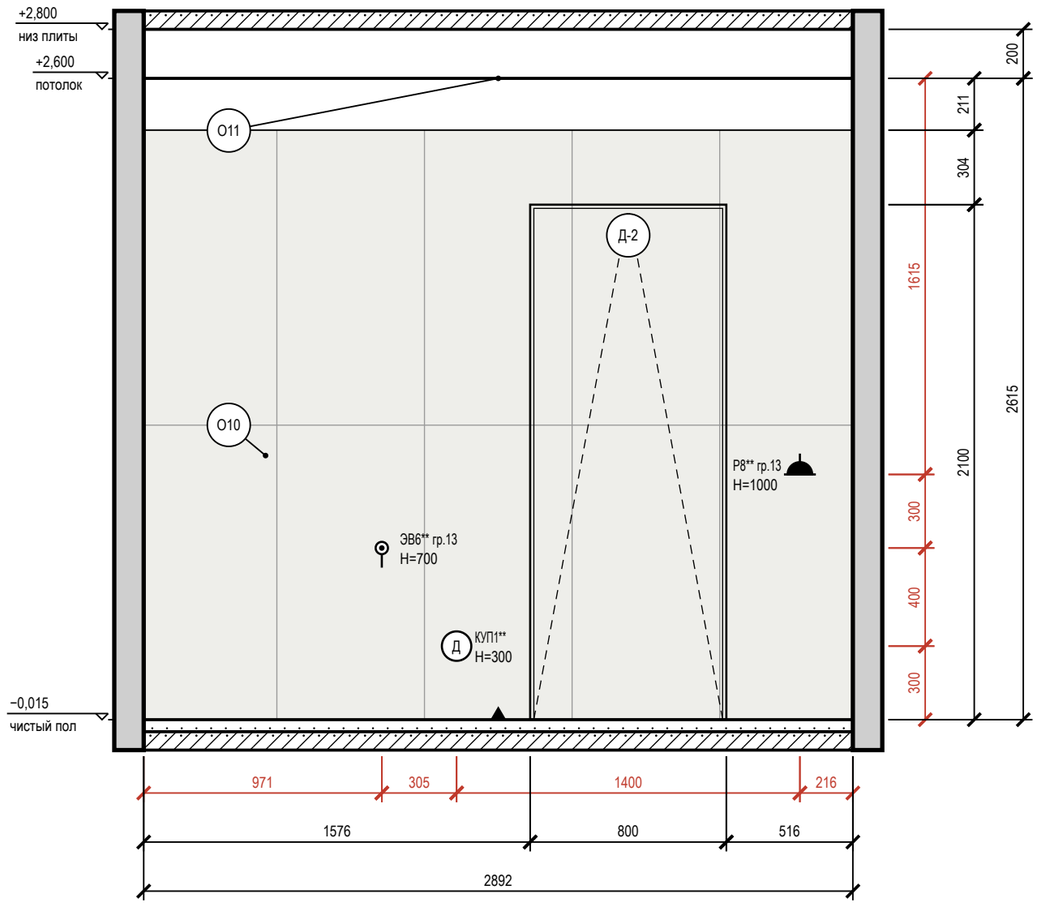

Условные обозначения

- розетка влагозащищённая IP44
- вывод кабеля для подключения прибора (без розетки), марка ЭВ
- привязки точек и выводов от угла и от пола, мм
- мебель и приборы — фасад по расстановке (условно)
- дверь скрытого монтажа: полотно в плоскости стены (узел — на листе узлов)
- стены и перекрытия в сечении
- плитка: сетка швов по формату, ▲ — ось старта
- О1 — марка отделки по реестру отделки альбома
- А — марка развёртки: буква стены, стрелка — взгляд

Допущения и предложения на листе

Основа листа: размеры и контуры этажей подобраны проектировщиком по составу помещений и площадям этажей с картинки 470 px (размеры на ней не читаются); обмер и исходный проект — задание (К-1); высоты: 1-й этаж 2800 мм, мансарда 2700 мм (горизонтальная часть) приняты; скаты кровли мансарды приняты по картинке: колено 1200 мм, уклон 45°, конёк вдоль длинной стороны; проект КР — задание (К-2); наружные стены 400 мм, перегородки 120 мм приняты (К-1); разрешённая мощность 15 кВт принята по типовым ТУ для частного дома (К-4); подрайон климата не задан — принят не северный (жилые от 2,5 м) (К-7).

Знак «**» — предложение проектировщика, заказчиком не утверждено (согласовать с заказчиком): записи в реестре нет: Р8 — по образцу: Р7, Р8 и Р33 на высоте 1000 мм — верхний предел нормы (ПУЭ, п. 6.6.30, не выше 1 м); флаг решения снят; КУП1 — по образцу: Добавлены выводы к вентиляторам: ЭВ4 (ВР1, ванная) и ЭВ5 (ВР3, санузел 2) — группа 3, высота 2389 мм, включение с основным светом, таймер выбега в вентиляторе; и коробки уравнивания потенциалов КУП1 (ванная) и КУП2 (санузел 2) — высота 300 мм, у входа, вне зон 0–2, проводник от шины РЕ щита ЩК, сече; ЭВ6 — по образцу: Добавлены электрические полотенцесушители IP44: П10 в ванной (480 мм, низ 900 мм) и П13 в санузле 2 (400 мм, низ 900 мм), выводы ЭВ6 и ЭВ7; мощность группы 13 — 2,4 кВт вместо 1,8 кВт.

См. лист открытых вопросов (лист 7, записи К-1, К-2, К-4, К-7).

Схема развёрток (М 1:100)

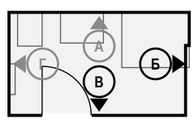

Ведомость отделки (на листе)

Марка	Поверхность	Материал, изделие	Цвет, код	Кол.
О10	стены	облицовка плиткой, Atlas Concorde Marvel Travertine, 600×1200×9 мм, A8UZ, затирка CG2WA	Atlas Concorde A8UZ «Marvel Travertine»	9,2 м²
О11	потолок	окраска, Tikkurila Luja 7, матовая, подготовка Q3	Little Greene No. 105 «Slaked Lime»	4,9 м²

Примечания

1. Развёртки — вид на стену изнутри помещения, по часовой стрелке; расположение — на схеме листа и на листе 102; размеры — в мм по чистовым поверхностям; отметки — в м от ±0,000; высоты Н — от чистого пола помещения до оси изделия, у декора — до центра.
2. Красные цепочки — привязки электроточек и выводов: по горизонтали от угла чистовых стен, по вертикали от чистого пола, до оси изделия; звенья короче 3 мм на листе вынесены во второй ярус (ближняя к стене цепочка).
3. У знака электроточки: марка (Р — розетка, S — выключатель, Св — светильник, ЭВ — вывод кабеля), ×N — число постов в рамке, гр. — группа щита, Н — высота оси от чистого пола, мм; группы по клавишам выключателя — на листе выключателей.
4. Схема мебели, приборов и декора не является технической документацией для производства мебели; габариты — по паспортам изделий (* — высота не задана в проекте, показана по типовому изделию).
5. Облицовка — по сетке швов 2 мм, раскладка от оси стены (треугольник у пола), целые ряды от пола; подрезки — по листу раскладки плитки.
6. Гидроизоляция в 2 слоя, заход на стены 200 мм — до облицовки, с актом скрытых работ и тестом проливом (узел — на листе узлов).
7. Двери скрытого монтажа — полотно в плоскости стены, отделка стены по полотну, плинтус прерывается у короба (узел — на листе узлов).

1000 мм · печать 1:1

Изм.	Кол.уч	Лист	№ док.	Подп.	Дата
Разраб.		Кырлан А.С.			21.10.26
Пров.					
ГИП					
Н. контр.					
Утв.					

ГД-2026-010-АИ

Дом 331 м²

Общая площадь 270,67* м² · * размеры приняты, не замерены (реестр — л. 7, К-1)

Дизайн-проект интерьера	Стадия	Лист	Листов
	РП	109	159

Развёртки стен Б, В. Санузел 1 этажа (пом. 3)

М 1:25

Кырлан Александр Сергеевич

выпуск 18.10.2026 № 9365d64cec · стр. 115 из 197

Развёртка стены Г. Санузел 1 этажа (пом. 3)

Санузел 1 этажа (пом. 3) · вид изнутри помещения · размеры в мм, отметки в м

ПРЕДВАРИТЕЛЬНО · не для производства работ · открыто пунктов: 6 (реестр — л. 7)

Развёртка стены Г

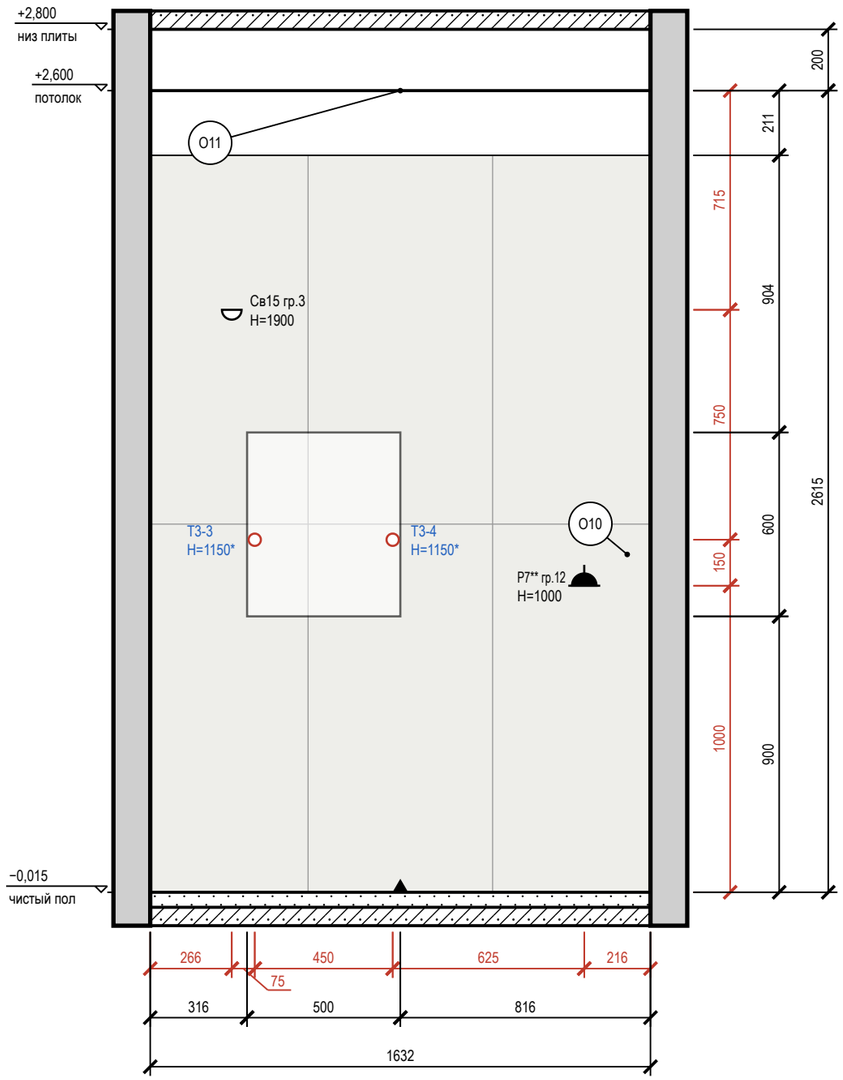

Схема развёрток (М 1:100)

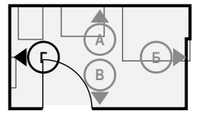

Условные обозначения

- розетка влагозащищённая IP44
- светильник настенный (бра), H — высота оси
- вывод Т3 (код — в ведомости привязок)
- привязки точек и выводов от угла и от пола, мм
- мебель и приборы — фасад по расстановке (условно)
- стены и перекрытия в сечении
- плитка: сетка швов по формату, ▲ — ось старта
- О1 — марка отделки по реестру отделки альбома
- А — марка развёртки: буква стены, стрелка — взгляд

Ведомость отделки (на листе)

Марка	Поверхность	Материал, изделие	Цвет, код	Кол.
О10	стены	облицовка плиткой, Atlas Concorde Marvel Travertine, 600×1200×9 мм, A8UZ, затирка CG2WA	Atlas Concorde A8UZ «Marvel Travertine»	3,9 м²
О11	потолок	окраска, Tikkurila Luja 7, матовая, подготовка Q3	Little Greene No. 105 «Slaked Lime»	4,9 м²

Допущения и предложения на листе

Основа листа: размеры и контуры этажей подобраны проектировщиком по составу помещений и площадям этажей с картинки 470 px (размеры на ней не читаются); обмер и исходный проект — задание (К-1); высоты: 1-й этаж 2800 мм, мансарда 2700 мм (горизонтальная часть) приняты; скаты кровли мансарды приняты по картинке: колено 1200 мм, уклон 45°, конёк вдоль длинной стороны; проект КР — задание (К-2); наружные стены 400 мм, перегородки 120 мм приняты (К-1); разрешённая мощность 15 кВт принята по типовым ТУ для частного дома (К-4); подрайон климата не задан — принят не северный (жилые от 2,5 м) (К-7).

Знак «**» — предложение проектировщика, заказчиком не утверждено (согласовать с заказчиком): записи в реестре нет: Р7 — по образцу: Р7, Р8 и Р33 на высоте 1000 мм — верхний предел нормы (ПУЭ, п. 6.6.30, не выше 1 м); флаг решения снят.

См. лист открытых вопросов (лист 7, записи К-1, К-2, К-4, К-7).

Примечания

1. Развёртки — вид на стену изнутри помещения, по часовой стрелке; расположение — на схеме листа и на листе 102; размеры — в мм по чистовым поверхностям; отметки — в м от ±0,000; высоты H — от чистого пола помещения до оси изделия, у декора — до центра.
2. Красные цепочки — привязки электроточек и выводов: по горизонтали от угла чистовых стен, по вертикали от чистого пола, до оси изделия; звенья короче 3 мм на листе вынесены во второй ярус (ближняя к стене цепочка).
3. У знака электроточки: марка (Р — розетка, S — выключатель, Св — светильник, ЭВ — вывод кабеля), ×N — число постов в рамке, гр. — группа щита, H — высота оси от чистого пола, мм; группы по клавишам выключателя — на листе выключателей.
4. Схема мебели, приборов и декора не является технической документацией для производства мебели; габариты — по паспортам изделий (* — высота не задана в проекте, показана по типовому изделию).
5. Выводы ВК — коды и высоты по листу выводов сантехники; * — высота принята по типовой практике монтажа, окончательно — по паспорту прибора.
6. Облицовка — по сетке швов 2 мм, раскладка от оси стены (треугольник у пола), целые ряды от пола; подрезки — по листу раскладки плитки.
7. Гидроизоляция в 2 слоя, заход на стены 200 мм — до облицовки, с актом скрытых работ и тестом проливом (узел — на листе узлов).

1000 мм · печать 1:1

Изм.	Кол.уч	Лист	№ док.	Подп.	Дата
Разраб.		Кырлан А.С.			21.10.26
Пров.					
ГИП					
Н. контр.					
Утв.					

ГД-2026-010-АИ

Дом 331 м²

Общая площадь 270,67* м² · * размеры приняты, не замерены (реестр — л. 7, К-1)

Дизайн-проект интерьера

Стадия	Лист	Листов
РП	110	159

Развёртка стены Г. Санузел 1 этажа (пом. 3)

М 1:20

Кырлан Александр Сергеевич

выпуск 18.10.2026 № 9365d64cec · стр. 116 из 197

Развёртки стен. Котельная (пом. 4)

Котельная (пом. 4) · вид изнутри помещения · размеры в мм, отметки в м

ПРЕДВАРИТЕЛЬНО · не для производства работ · открыто пунктов: 6 (реестр — л. 7)

Развёртка стены А

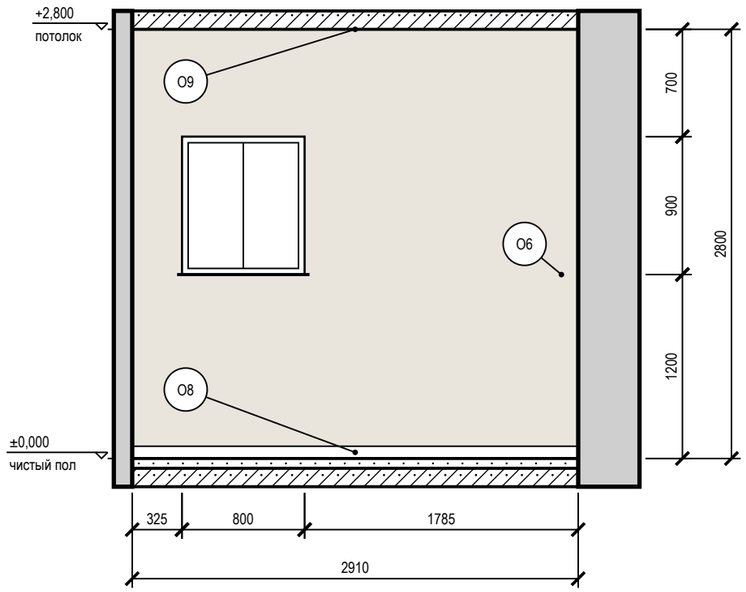

Развёртка стены Б

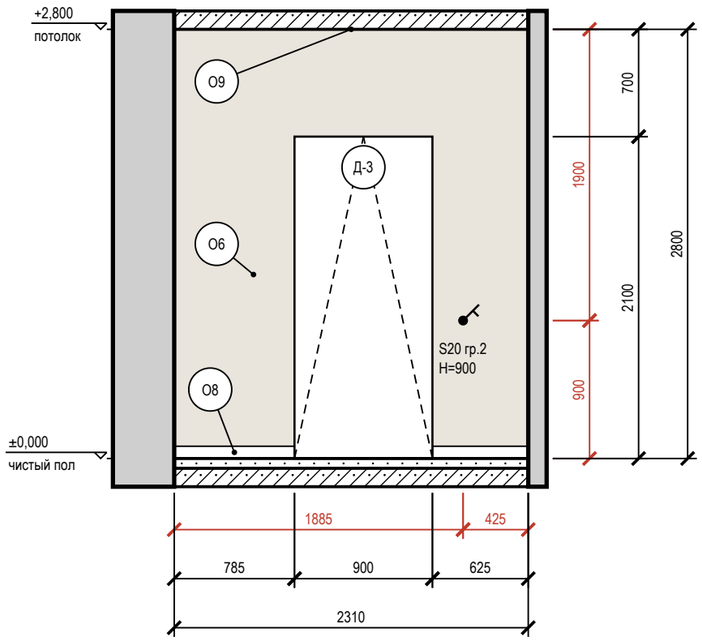

Развёртка стены Г

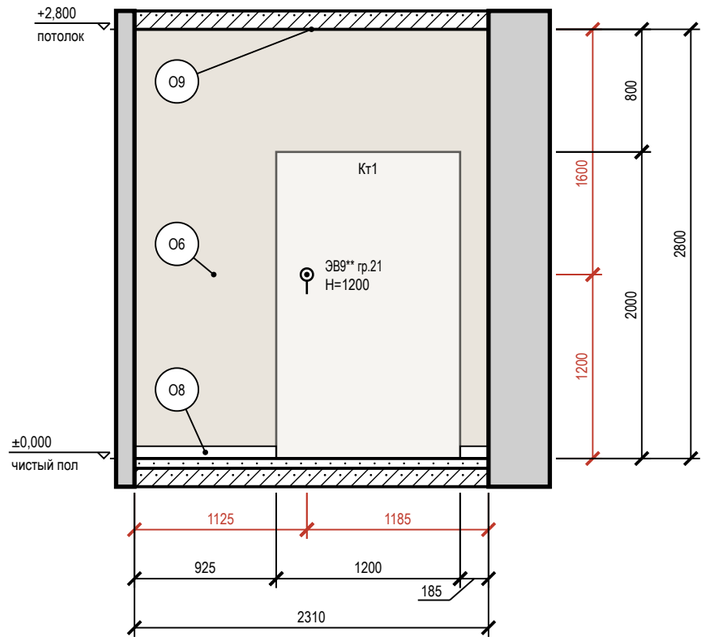

Схема развёрток (М 1:100)

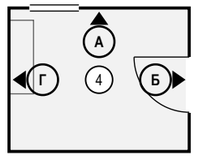

Условные обозначения

- вывод кабеля для подключения прибора (без розетки), марка ЭВ
- выключатель одноклавишный
- привязки точек и выводов от угла и от пола, мм
- мебель и приборы — фасад по расстановке (условно)
- окно: проём, рама, подоконник
- дверной проём; марка двери — в кружке
- стены и перекрытия в сечении
- окраска: тон — цвет по коду производителя (условно)
- О1 — марка отделки по реестру отделки альбома
- А — марка развёртки: буква стены, стрелка — взгляд

Ведомость отделки (на листе)

Марка	Поверхность	Материал, изделие	Цвет, код	Кол.
О6	стены	окраска, Farrow & Ball Modern Emulsion, матовая, подготовка Q3	Farrow & Ball No. 226 «Joa's White»	18,5 м²
О8	плинтус	плинтус МДФ, h 80 мм, аналог: плинтус МДФ под покраску 80×16	Farrow & Ball No. 226 «Joa's White»	5,4 м
О9	потолок	окраска, Tikkurila Anti-Reflex 2, глубокоматовая, подготовка Q3	Little Greene No. 105 «Slaked Lime»	6,9 м²

Допущения и предложения на листе

Основа листа: размеры и контуры этажей подобраны проектировщиком по составу помещений и площадям этажей с картинки 470 px (размеры на ней не читаются); обмер и исходный проект — задание (К-1); высоты: 1-й этаж 2800 мм, мансарда 2700 мм (горизонтальная часть) приняты; скаты кровли мансарды приняты по картинке: колено 1200 мм, уклон 45°, конёк вдоль длинной стороны; проект КР — задание (К-2); наружные стены 400 мм, перегородки 120 мм приняты (К-1); разрешённая мощность 15 кВт принята по типовым ТУ для частного дома (К-4); подрайон климата не задан — принят не северный (жилые от 2,5 м) (К-7).

Знак «**» — предложение проектировщика, заказчиком не утверждено (согласовать с заказчиком): записи в реестре нет: ЭВ9 — место и тип котла не выбраны (газ / электро — вопрос заказчику): вывод у стены D, уточнить по проекту котельной.

См. лист открытых вопросов (лист 7, записи К-1, К-2, К-4, К-7).

Примечания

1. Развёртки — вид на стену изнутри помещения, по часовой стрелке; расположение — на схеме листа и на листе 102; размеры — в мм по чистовым поверхностям; отметки — в м от ±0,000; высоты Н — от чистого пола помещения до оси изделия, у декора — до центра.
2. Красные цепочки — привязки электроточек и выводов: по горизонтали от угла чистовых стен, по вертикали от чистого пола, до оси изделия; звенья короче 3 мм на листе вынесены во второй ярус (ближняя к стене цепочка).
3. У знака электроточки: марка (Р — розетка, S — выключатель, Св — светильник, ЭВ — вывод кабеля), ×N — число постов в рамке, гр. — группа щита, Н — высота оси от чистого пола, мм; группы по клавишам выключателя — на листе выключателей.
4. Схема мебели, приборов и декора не является технической документацией для производства мебели; габариты — по паспортам изделий.

1000 мм · печать 1:1

Изм.	Кол.уч	Лист	№ док.	Подп.	Дата
Разраб.		Кырлан А.С.			21.10.26
Пров.					
ГИП					
Н. контр.					
Утв.					

ГД-2026-010-АИ

Дом 331 м²

Общая площадь 270,67* м² · * размеры приняты, не замерены (реестр — л. 7, К-1)

Дизайн-проект интерьера

Стадия	Лист	Листов
РП	111	159

Развёртки стен. Котельная (пом. 4)

М 1:40

Кырлан Александр Сергеевич

выпуск 18.10.2026 № 9365d64cec · стр. 117 из 197

Развёртка стены А. Гостиная (пом. 5)

Гостиная (пом. 5) · вид изнутри помещения · размеры в мм, отметки в м

ПРЕДВАРИТЕЛЬНО · не для производства работ · открыто пунктов: 6 (реестр — л. 7)

Развёртка стены А

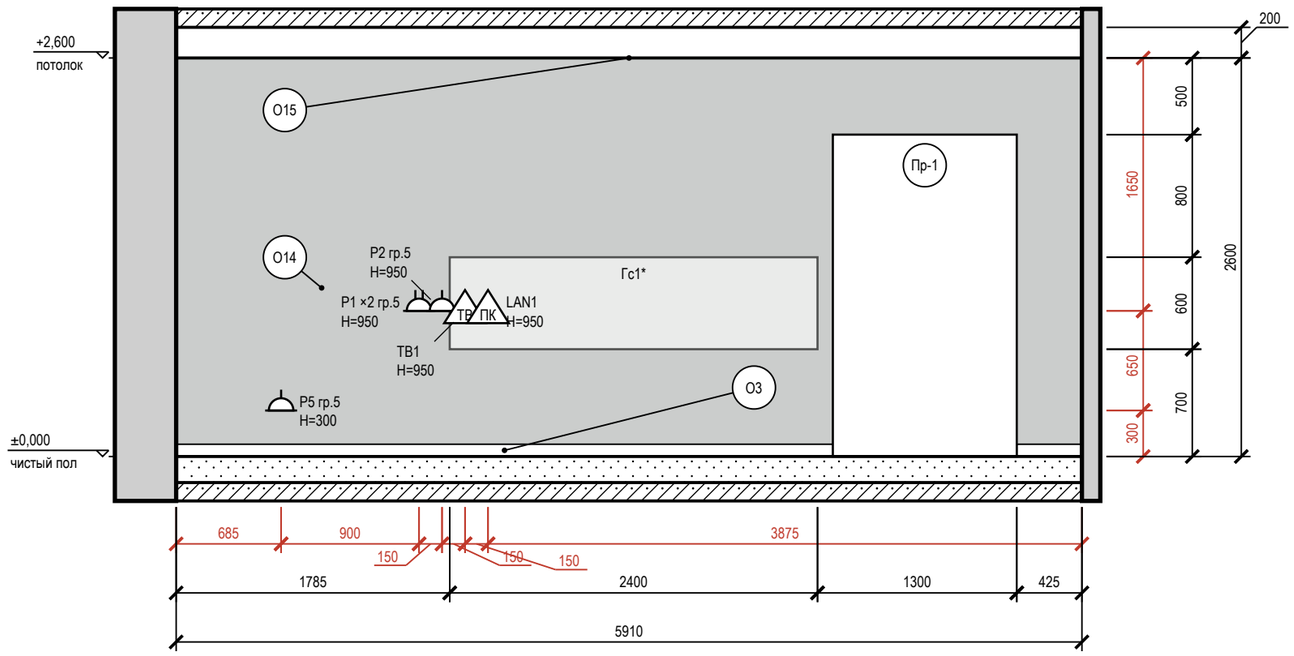

Условные обозначения

- розетка с заземляющим контактом; у знака — марка, ×N постов в рамке, гр. — группа щита, H — высота оси, мм
- ПК — розетка компьютерная RJ45
- ТВ — розетка телевизионная
- привязки точек и выводов от угла и от пола, мм
- мебель и приборы — фасад по расстановке (условно)
- дверной проём; марка двери — в кружке
- стены и перекрытия в сечении
- окраска: тон — цвет по коду производителя (условно)
- О1 — марка отделки по реестру отделки альбома
- А — марка развёртки: буква стены, стрелка — взгляд

Схема развёрток (М 1:100)

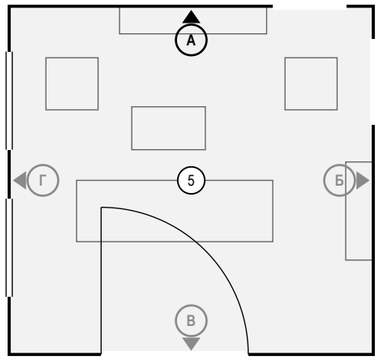

Ведомость отделки (на листе)

Марка	Поверхность	Материал, изделие	Цвет, код	Кол.
О3	плинтус	плинтус МДФ, h 80 мм, аналог: плинтус МДФ под окраску 80×16 мм, полуглянцевая	NCS S 0804-Y30R «S 0804-Y30R»	4,7 м
О14	акцентная стена	окраска, Tikkurila Optiva 5 Matt, аналог: интерьерная краска, класс 2 по EN 13300, глубокоматовая/матовая, база С, матовая, подготовка К3	Farrow & Ball No. 93 «Studio Green — почти чёрный зелёный»	12,8 м²
О15	потолок	окраска, Tikkurila Anti-Reflex 2, глубокоматовая, подготовка Q3	NCS S 0804-Y30R «S 0804-Y30R»	33,7 м²

Допущения и предложения на листе

Основа листа: размеры и контуры этажей подобраны проектировщиком по составу помещений и площадям этажей с картинки 470 px (размеры на ней не читаются); обмер и исходный проект — задание (К-1); высоты: 1-й этаж 2800 мм, мансарда 2700 мм (горизонтальная часть) приняты; скаты кровли мансарды приняты по картинке: колено 1200 мм, уклон 45°, конёк вдоль длинной стороны; проект КР — задание (К-2); наружные стены 400 мм, перегородки 120 мм приняты (К-1); разрешённая мощность 15 кВт принята по типовым ТУ для частного дома (К-4); подрайон климата не задан — принят не северный (жилые от 2,5 м) (К-7).

См. лист открытых вопросов (лист 7, записи К-1, К-2, К-4, К-7).

Примечания

1. Развёртки — вид на стену изнутри помещения, по часовой стрелке; расположение — на схеме листа и на листе 102; размеры — в мм по чистовым поверхностям; отметки — в м от ±0,000; высоты H — от чистого пола помещения до оси изделия, у декора — до центра.
2. Красные цепочки — привязки электроточек и выводов: по горизонтали от угла чистовых стен, по вертикали от чистого пола, до оси изделия; звенья короче 3 мм на листе вынесены во второй ярус (ближняя к стене цепочка).
3. У знака электроточки: марка (Р — розетка, S — выключатель, Св — светильник, ЭВ — вывод кабеля), ×N — число постов в рамке, гр. — группа щита, H — высота оси от чистого пола, мм; группы по клавишам выключателя — на листе выключателей.
4. Схема мебели, приборов и декора не является технической документацией для производства мебели; габариты — по паспортам изделий (* — высота не задана в проекте, показана по типовому изделию).
5. Потолок на развёртках — по нижнему уровню У1; другие уровни потолка помещения: У2 +2,700.

1000 мм · печать 1:1

Изм.	Кол.уч	Лист	№ док.	Подп.	Дата
Разраб.		Кырлан А.С.			21.10.26
Пров.					
ГИП					
Н. контр.					
Утв.					

ГД-2026-010-АИ

Дом 331 м²

Общая площадь 270,67* м² · * размеры приняты, не замерены (реестр — л. 7, К-1)

Дизайн-проект интерьера

Стадия	Лист	Листов
РП	112	159

Развёртка стены А. Гостиная (пом. 5)

М 1:40

Кырлан Александр Сергеевич

выпуск 18.10.2026 № 9365d64cec · стр. 118 из 197

Развёртка стены Б. Гостиная (пом. 5)

Гостиная (пом. 5) · вид изнутри помещения · размеры в мм, отметки в м

ПРЕДВАРИТЕЛЬНО · не для производства работ · открыто пунктов: 6 (реестр — л. 7)

Развёртка стены Б

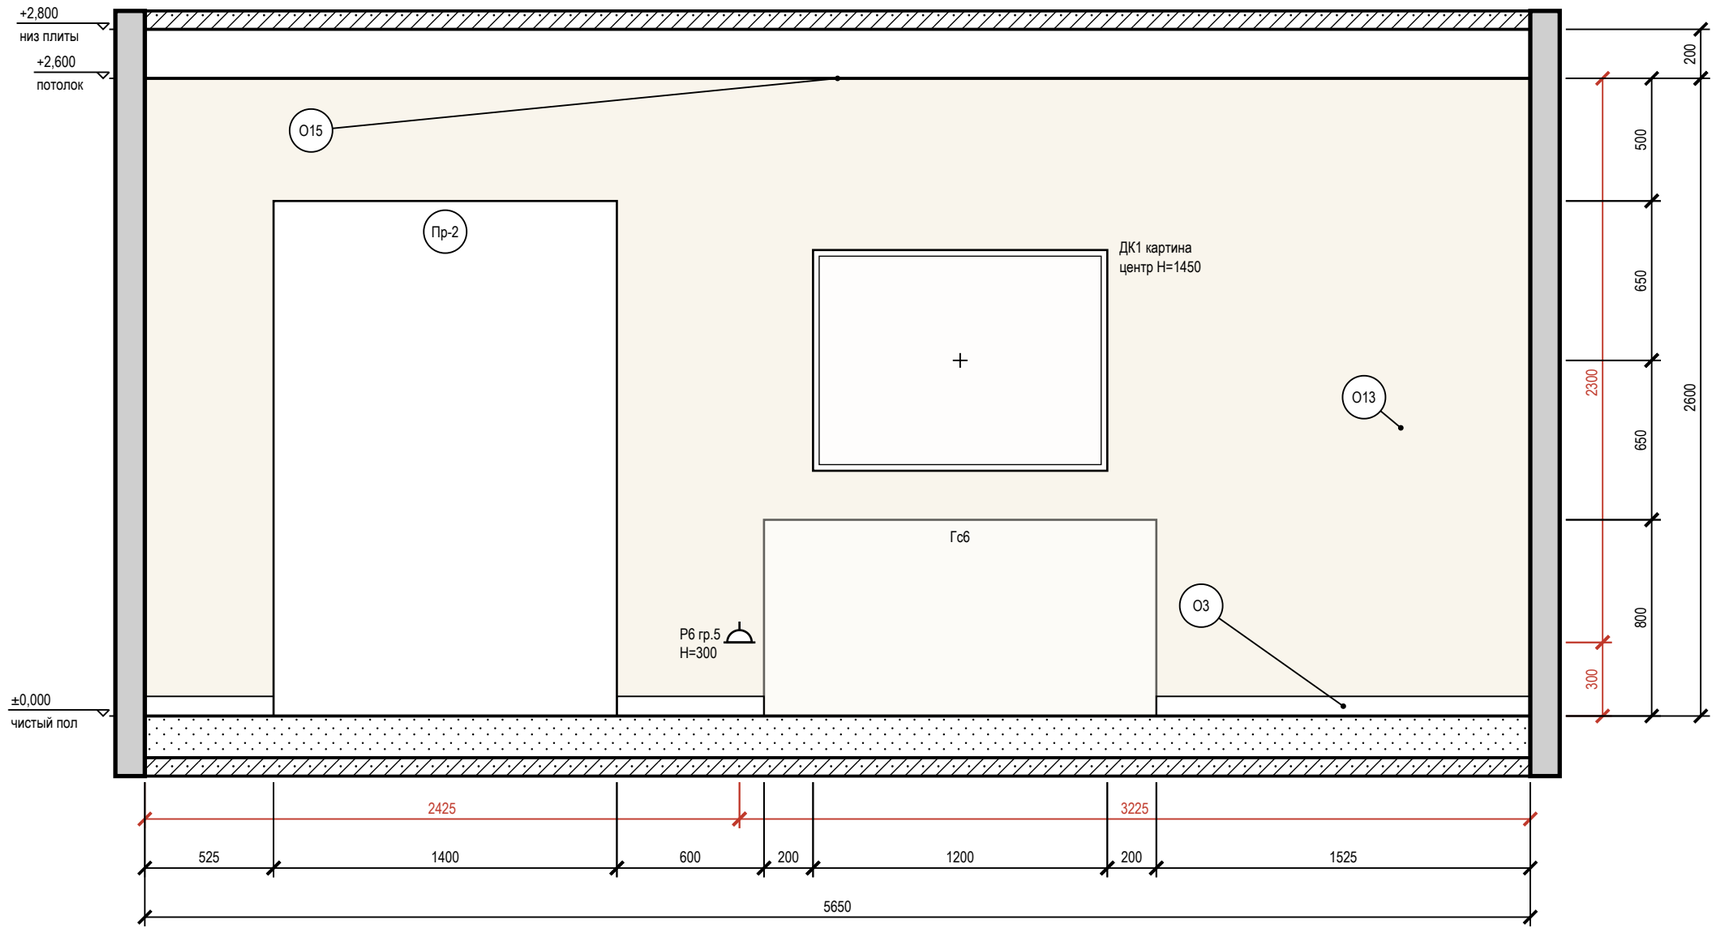

Схема развёрток (М 1:100)

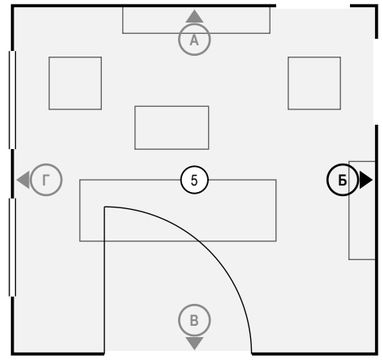

Условные обозначения

- розетка с заземляющим контактом; у знака — марка, ×N постов в рамке, гр. — группа щита, Н — высота оси, мм
- привязки точек и выводов от угла и от пола, мм
- мебель и приборы — фасад по расстановке (условно)
- картина (декор): марка Д, крест — центр, Н — высота центра, мм
- дверной проём; марка двери — в кружке
- стены и перекрытия в сечении
- окраска: тон — цвет по коду производителя (условно)
- О1 — марка отделки по реестру отделки альбома
- А — марка развёртки: буква стены, стрелка — взгляд

Допущения и предложения на листе

Основа листа: размеры и контуры этажей подобраны проектировщиком по составу помещений и площадям этажей с картинки 470 px (размеры на ней не читаются); обмер и исходный проект — задание (К-1); высоты: 1-й этаж 2800 мм, мансарда 2700 мм (горизонтальная часть) приняты; скаты кровли мансарды приняты по картинке: колено 1200 мм, уклон 45°, конёк вдоль длинной стороны; проект КР — задание (К-2); наружные стены 400 мм, перегородки 120 мм приняты (К-1); разрешённая мощность 15 кВт принята по типовым ТУ для частного дома (К-4); подрайон климата не задан — принят не северный (жилые от 2,5 м) (К-7).

См. лист открытых вопросов (лист 7, записи К-1, К-2, К-4, К-7).

Примечания

1. Развёртки — вид на стену изнутри помещения, по часовой стрелке; расположение — на схеме листа и на листе 102; размеры — в мм по чистовым поверхностям; отметки — в м от ±0,000; высоты Н — от чистого пола помещения до оси изделия, у декора — до центра.
2. Красные цепочки — привязки электроточек и выводов: по горизонтали от угла чистовых стен, по вертикали от чистого пола, до оси изделия; звенья короче 3 мм на листе вынесены во второй ярус (ближняя к стене цепочка).
3. У знака электроточки: марка (Р — розетка, S — выключатель, Св — светильник, ЭВ — вывод кабеля), ×N — число постов в рамке, гр. — группа щита, Н — высота оси от чистого пола, мм; группы по клавишам выключателя — на листе выключателей.
4. Схема мебели, приборов и декора не является технической документацией для производства мебели; габариты — по паспортам изделий.
5. Картины и зеркала крепить к основанию по паспорту изделия (закладные и анкеры — в перечне скрытых работ); крест — ось центра предмета.
6. Потолок на развёртках — по нижнему уровню У1; другие уровни потолка помещения: У2 +2,700.

1000 мм · печать 1:1

Изм.	Кол.уч	Лист	№ док.	Подп.	Дата
Разраб.		Кырлан А.С.			21.10.26
Пров.					
ГИП					
Н. контр.					
Утв.					

ГД-2026-010-АИ

Дом 331 м²

Общая площадь 270,67* м² · * размеры приняты, не замерены (реестр — л. 7, К-1)

Дизайн-проект интерьера

Стадия	Лист	Листов
РП	113	159

Развёртка стены Б. Гостиная (пом. 5)

М 1:25

Кырлан Александр Сергеевич

выпуск 18.10.2026 № 9365d64cec · стр. 119 из 197

Развёртка стены В. Гостиная (пом. 5)

Гостиная (пом. 5) · вид изнутри помещения · размеры в мм, отметки в м

ПРЕДВАРИТЕЛЬНО · не для производства работ · открыто пунктов: 6 (реестр — л. 7)

Развёртка стены В

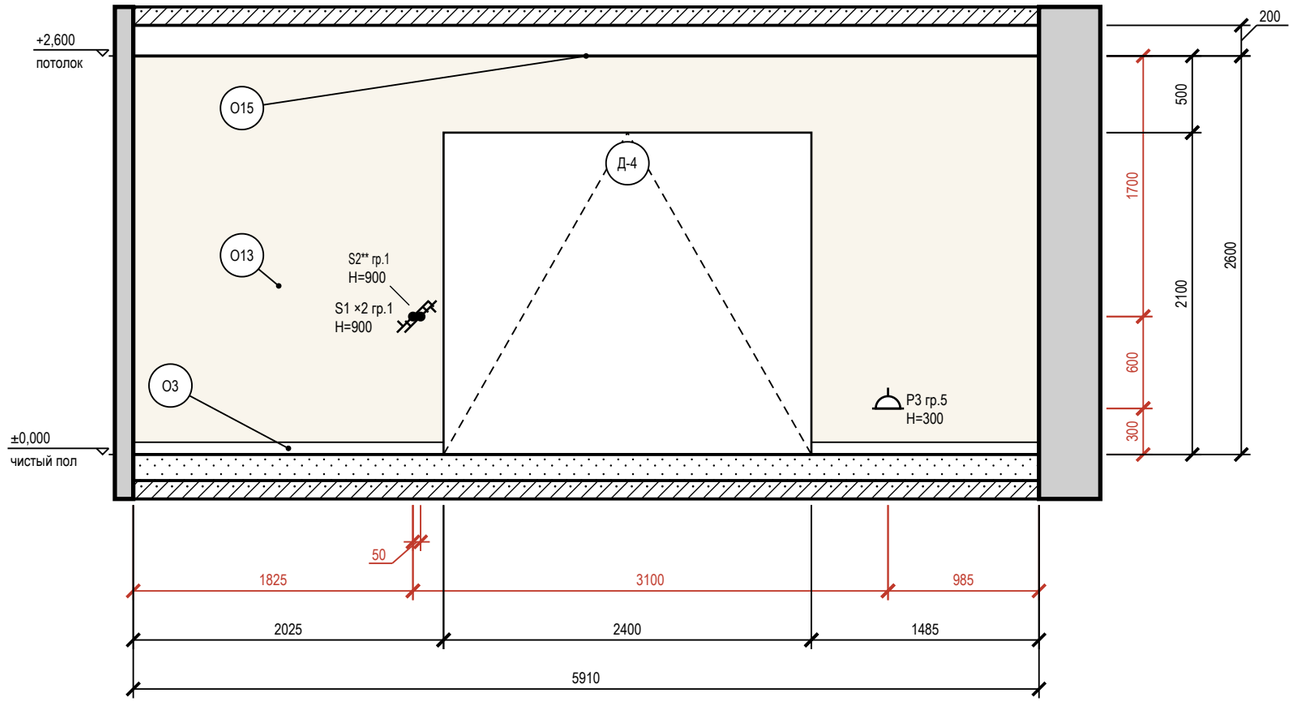

Условные обозначения

- розетка с заземляющим контактом; у знака — марка, ×N постов в рамке, гр. — группа щита, H — высота оси, мм
- выключатель одноклавишный
- выключатель двухклавишный (флажков — по числу клавиш)
- выключатель с проходной или перекрёстной клавишей (обратный флажок); тип клавиши — в подписи
- привязки точек и выводов от угла и от пола, мм
- мебель и приборы — фасад по расстановке (условно)
- дверной проём; марка двери — в кружке
- стены и перекрытия в сечении
- окраска: тон — цвет по коду производителя (условно)
- О1 — марка отделки по реестру отделки альбома
- A — марка развёртки: буква стены, стрелка — взгляд

Схема развёрток (М 1:100)

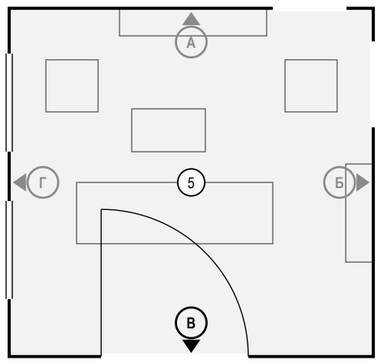

Ведомость отделки (на листе)

Марка	Поверхность	Материал, изделие	Цвет, код	Кол.
О3	плинтус	плинтус МДФ, h 80 мм, аналог: плинтус МДФ под окраску 80×16 мм, полуглянцевая	NCS S 0804-Y30R «S 0804-Y30R»	3,5 м
О13	стены	окраска, Tikkurila Optiva 5 Matt, матовая, подготовка К3	NCS S 0804-Y30R «S 0804-Y30R»	10,3 м²
О15	потолок	окраска, Tikkurila Anti-Reflex 2, глубокоматовая, подготовка Q3	NCS S 0804-Y30R «S 0804-Y30R»	33,7 м²

Допущения и предложения на листе

Основа листа: размеры и контуры этажей подобраны проектировщиком по составу помещений и площадям этажей с картинки 470 px (размеры на ней не читаются); обмер и исходный проект — задание (К-1); высоты: 1-й этаж 2800 мм, мансарда 2700 мм (горизонтальная часть) приняты; скаты кровли мансарды приняты по картинке: колено 1200 мм, уклон 45°, конёк вдоль длинной стороны; проект КР — задание (К-2); наружные стены 400 мм, перегородки 120 мм приняты (К-1); разрешённая мощность 15 кВт принята по типовым ТУ для частного дома (К-4); подрайон климата не задан — принят не северный (жилые от 2,5 м) (К-7).

Знак «**» — предложение проектировщика, заказчиком не утверждено (согласовать с заказчиком): записи в реестре нет: S2 — светорегулятор добавлен под диммируемую ленту L3; уровни сценариев выбраны конвейером.

См. лист открытых вопросов (лист 7, записи К-1, К-2, К-4, К-7).

Примечания

1. Развёртки — вид на стену изнутри помещения, по часовой стрелке; расположение — на схеме листа и на листе 102; размеры — в мм по чистовым поверхностям; отметки — в м от ±0,000; высоты H — от чистого пола помещения до оси изделия, у декора — до центра.
2. Красные цепочки — привязки электроточек и выводов: по горизонтали от угла чистовых стен, по вертикали от чистого пола, до оси изделия; звенья короче 3 мм на листе вынесены во второй ярус (ближняя к стене цепочка).
3. У знака электроточки: марка (Р — розетка, S — выключатель, Св — светильник, ЭВ — вывод кабеля), ×N — число постов в рамке, гр. — группа щита, H — высота оси от чистого пола, мм; группы по клавишам выключателя — на листе выключателей.
4. Схема мебели, приборов и декора не является технической документацией для производства мебели; габариты — по паспортам изделий.
5. Потолок на развёртках — по нижнему уровню У1; другие уровни потолка помещения: У2 +2,700.

1000 мм · печать 1:1

Изм.	Кол.уч	Лист	№ док.	Подп.	Дата
Разраб.		Кырлан А.С.			21.10.26
Пров.					
ГИП					
Н. контр.					
Утв.					

ГД-2026-010-АИ

Дом 331 м²

Общая площадь 270,67* м² · * размеры приняты, не замерены (реестр — л. 7, К-1)

Дизайн-проект интерьера

Стадия	Лист	Листов
РП	114	159

Развёртка стены В. Гостиная (пом. 5)

М 1:40

Кырлан Александр Сергеевич

выпуск 18.10.2026 № 9365d64cec · стр. 120 из 197

Развёртка стены Г. Гостиная (пом. 5)

Гостиная (пом. 5) · вид изнутри помещения · размеры в мм, отметки в м

ПРЕДВАРИТЕЛЬНО · не для производства работ · открыто пунктов: 6 (реестр — л. 7)

Развёртка стены Г

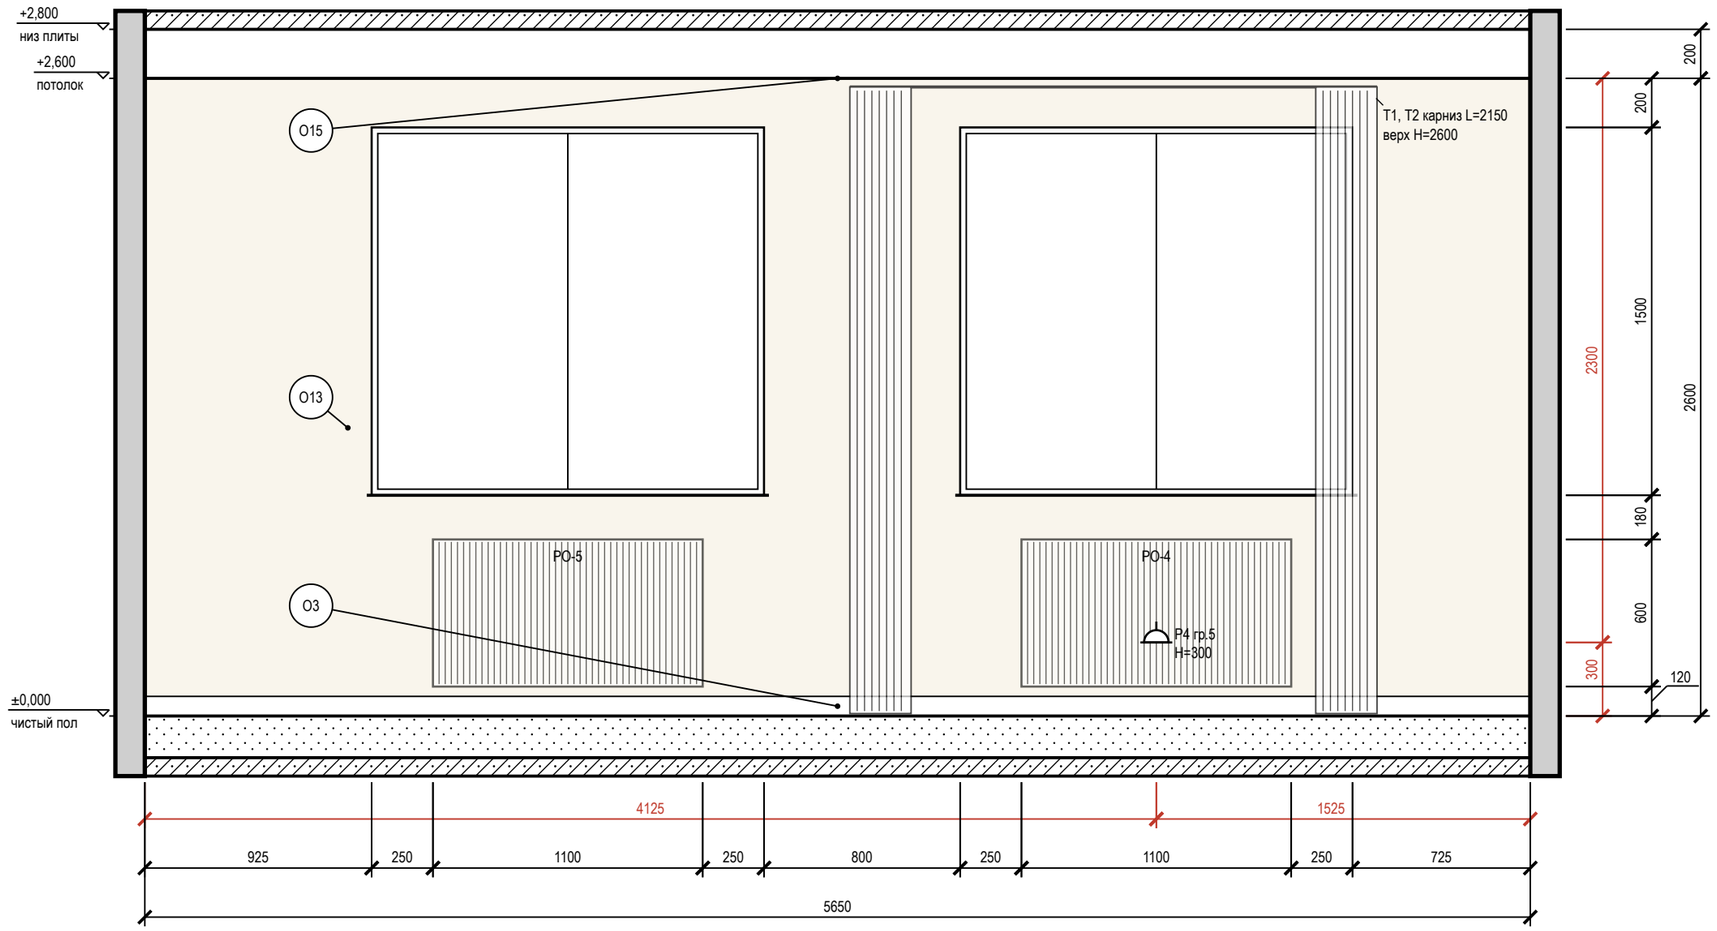

Схема развёрток (М 1:100)

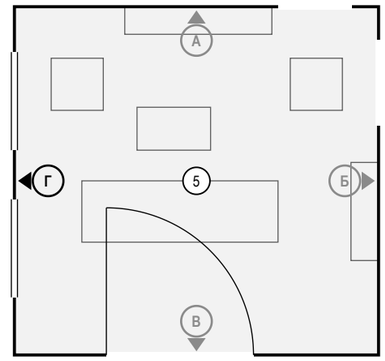

Условные обозначения

- розетка с заземляющим контактом; у знака — марка, ×N постов в рамке, гр. — группа щита, H — высота оси, мм
- привязки точек и выводов от угла и от пола, мм
- мебель и приборы — фасад по расстановке (условно)
- карниз (шина) и шторы в собранном виде: марка T, длина L, верх H
- окно: проём, рама, подоконник
- радиатор отопления; марка — по плану отопления
- стены и перекрытия в сечении
- окраска: тон — цвет по коду производителя (условно)
- О1 — марка отделки по реестру отделки альбома
- А — марка развёртки: буква стены, стрелка — взгляд

Допущения и предложения на листе

Основа листа: размеры и контуры этажей подобраны проектировщиком по составу помещений и площадям этажей с картинки 470 px (размеры на ней не читаются); обмер и исходный проект — задание (К-1); высоты: 1-й этаж 2800 мм, мансарда 2700 мм (горизонтальная часть) приняты; скаты кровли мансарды приняты по картинке: колено 1200 мм, уклон 45°, конёк вдоль длинной стороны; проект КР — задание (К-2); наружные стены 400 мм, перегородки 120 мм приняты (К-1); разрешённая мощность 15 кВт принята по типовым ТУ для частного дома (К-4); подрайон климата не задан — принят не северный (жилые от 2,5 м) (К-7).

См. лист открытых вопросов (лист 7, записи К-1, К-2, К-4, К-7).

Примечания

1. Развёртки — вид на стену изнутри помещения, по часовой стрелке; расположение — на схеме листа и на листе 102; размеры — в мм по чистовым поверхностям; отметки — в м от ±0,000; высоты H — от чистого пола помещения до оси изделия, у декора — до центра.
2. Красные цепочки — привязки электроточек и выводов: по горизонтали от угла чистовых стен, по вертикали от чистого пола, до оси изделия; звенья короче 3 мм на листе вынесены во второй ярус (ближняя к стене цепочка).
3. У знака электроточки: марка (Р — розетка, S — выключатель, Св — светильник, ЭВ — вывод кабеля), ×N — число постов в рамке, гр. — группа щита, H — высота оси от чистого пола, мм; группы по клавишам выключателя — на листе выключателей.
4. Схема мебели, приборов и декора не является технической документацией для производства мебели; габариты — по паспортам изделий.
5. Карнизы (шины) — по ведомости текстиля декоратора; длина L и верх H — по развёртке, крепление — до окраски потолка.
6. Потолок на развёртках — по нижнему уровню У1; другие уровни потолка помещения: У2 +2,700.

1000 мм · печать 1:1

Изм.	Кол.уч	Лист	№ док.	Подп.	Дата
Разраб.		Кырлан А.С.			21.10.26
Пров.					
ГИП					
Н. контр.					
Утв.					

ГД-2026-010-АИ

Дом 331 м²

Общая площадь 270,67* м² · * размеры приняты, не замерены (реестр — л. 7, К-1)

Дизайн-проект интерьера	Стадия	Лист	Листов
	РП	115	159

Развёртка стены Г. Гостиная (пом. 5)

М 1:25

Кырлан Александр Сергеевич

выпуск 18.10.2026 № 9365d64cec · стр. 121 из 197

Развёртки стен. Холл с лестницей (пом. 6)

Холл с лестницей (пом. 6) · вид изнутри помещения · размеры в мм, отметки в м

ПРЕДВАРИТЕЛЬНО · не для производства работ · открыто пунктов: 6 (реестр — л. 7)

Развёртка стены А

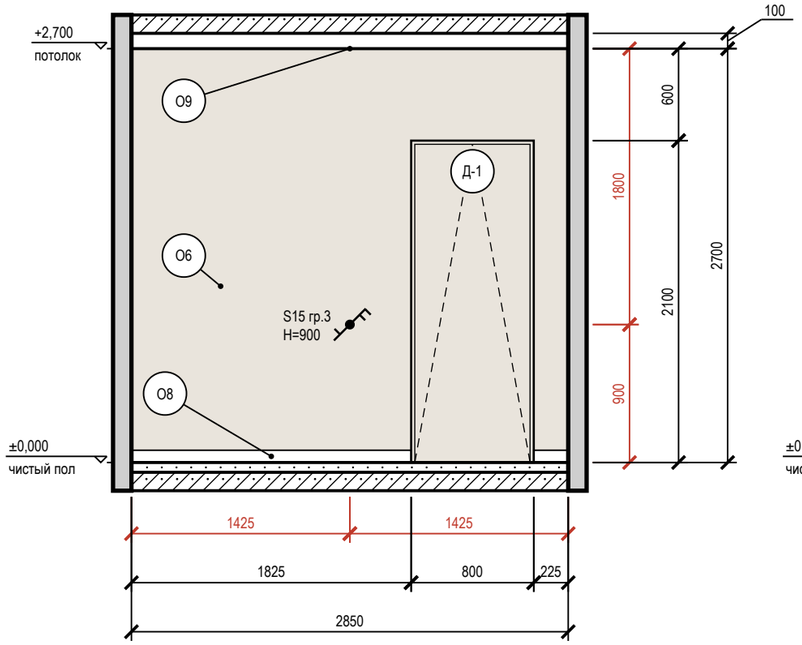

Развёртка стены В

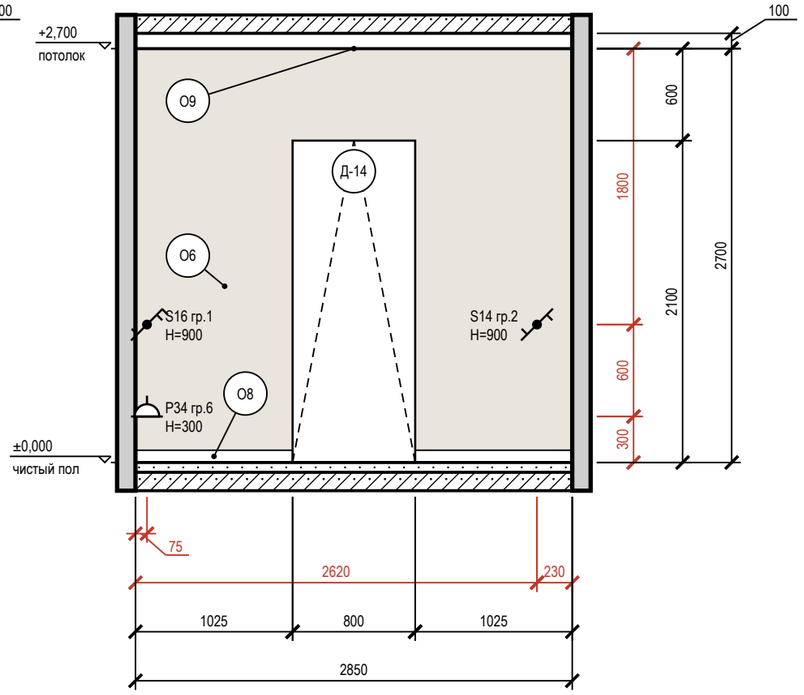

Схема развёрток (М 1:100)

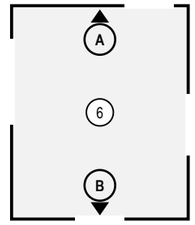

Условные обозначения

- розетка с заземляющим контактом; у знака — марка, ×N постов в рамке, гр. — группа щита, H — высота оси, мм
- выключатель одноклавишный
- выключатель двухклавишный (флажков — по числу клавиш)
- выключатель с проходной или перекрёстной клавишей (обратный флажок); тип клавиши — в подписи
- привязки точек и выводов от угла и от пола, мм
- мебель и приборы — фасад по расстановке (условно)
- дверь скрытого монтажа: полотно в плоскости стены (узел — на листе узлов)
- дверной проём; марка двери — в кружке
- стены и перекрытия в сечении
- окраска: тон — цвет по коду производителя (условно)
- О1 — марка отделки по реестру отделки альбома
- A — марка развёртки: буква стены, стрелка — взгляд

Ведомость отделки (на листе)

Марка	Поверхность	Материал, изделие	Цвет, код	Кол.
О6	стены	окраска, Farrow & Ball Modern Emulsion, матовая, подготовка Q3	Farrow & Ball No. 226 «Joa's White»	12 м²
О8	плинтус	плинтус МДФ, h 80 мм, аналог: плинтус МДФ под покраску 80×16	Farrow & Ball No. 226 «Joa's White»	4,1 м
О9	потолок	окраска, Tikkurila Anti-Reflex 2, глубокоматовая, подготовка Q3	Little Greene No. 105 «Slaked Lime»	10 м²

Допущения и предложения на листе

Основа листа: размеры и контуры этажей подобраны проектировщиком по составу помещений и площадям этажей с картинки 470 px (размеры на ней не читаются); обмер и исходный проект — задание (К-1); высоты: 1-й этаж 2800 мм, мансарда 2700 мм (горизонтальная часть) приняты; скаты кровли мансарды приняты по картинке: колено 1200 мм, уклон 45°, конёк вдоль длинной стороны; проект КР — задание (К-2); наружные стены 400 мм, перегородки 120 мм приняты (К-1); разрешённая мощность 15 кВт принята по типовым ТУ для частного дома (К-4); подрайон климата не задан — принят не северный (жилые от 2,5 м) (К-7).

См. лист открытых вопросов (лист 7, записи К-1, К-2, К-4, К-7).

Примечания

1. Развёртки — вид на стену изнутри помещения, по часовой стрелке; расположение — на схеме листа и на листе 102; размеры — в мм по чистовым поверхностям; отметки — в м от ±0,000; высоты H — от чистого пола помещения до оси изделия, у декора — до центра.
2. Красные цепочки — привязки электроточек и выводов: по горизонтали от угла чистовых стен, по вертикали от чистого пола, до оси изделия; звенья короче 3 мм на листе вынесены во второй ярус (ближняя к стене цепочка).
3. У знака электроточки: марка (Р — розетка, S — выключатель, Св — светильник, ЭВ — вывод кабеля), ×N — число постов в рамке, гр. — группа щита, H — высота оси от чистого пола, мм; группы по клавишам выключателя — на листе выключателей.
4. Схема мебели, приборов и декора не является технической документацией для производства мебели; габариты — по паспортам изделий.
5. Двери скрытого монтажа — полотно в плоскости стены, отделка стены по полотну, плинтус прерывается у короба (узел — на листе узлов).

1000 мм · печать 1:1

Изм.	Кол.уч	Лист	№ док.	Подп.	Дата
Разраб.		Кырлан А.С.			21.10.26
Пров.					
ГИП					
Н. контр.					
Утв.					

ГД-2026-010-АИ

Дом 331 м²

Общая площадь 270,67* м² · * размеры приняты, не замерены (реестр — л. 7, К-1)

Дизайн-проект интерьера

Стадия	Лист	Листов
РП	116	159

Развёртки стен. Холл с лестницей (пом. 6)

М 1:40

Кырлан Александр Сергеевич

выпуск 18.10.2026 № 9365d64cec · стр. 122 из 197

Развёртки стен. Кладовая (пом. 7)

Кладовая (пом. 7) · вид изнутри помещения · размеры в мм, отметки в м

ПРЕДВАРИТЕЛЬНО · не для производства работ · открыто пунктов: 6 (реестр — л. 7)

Развёртка стены В

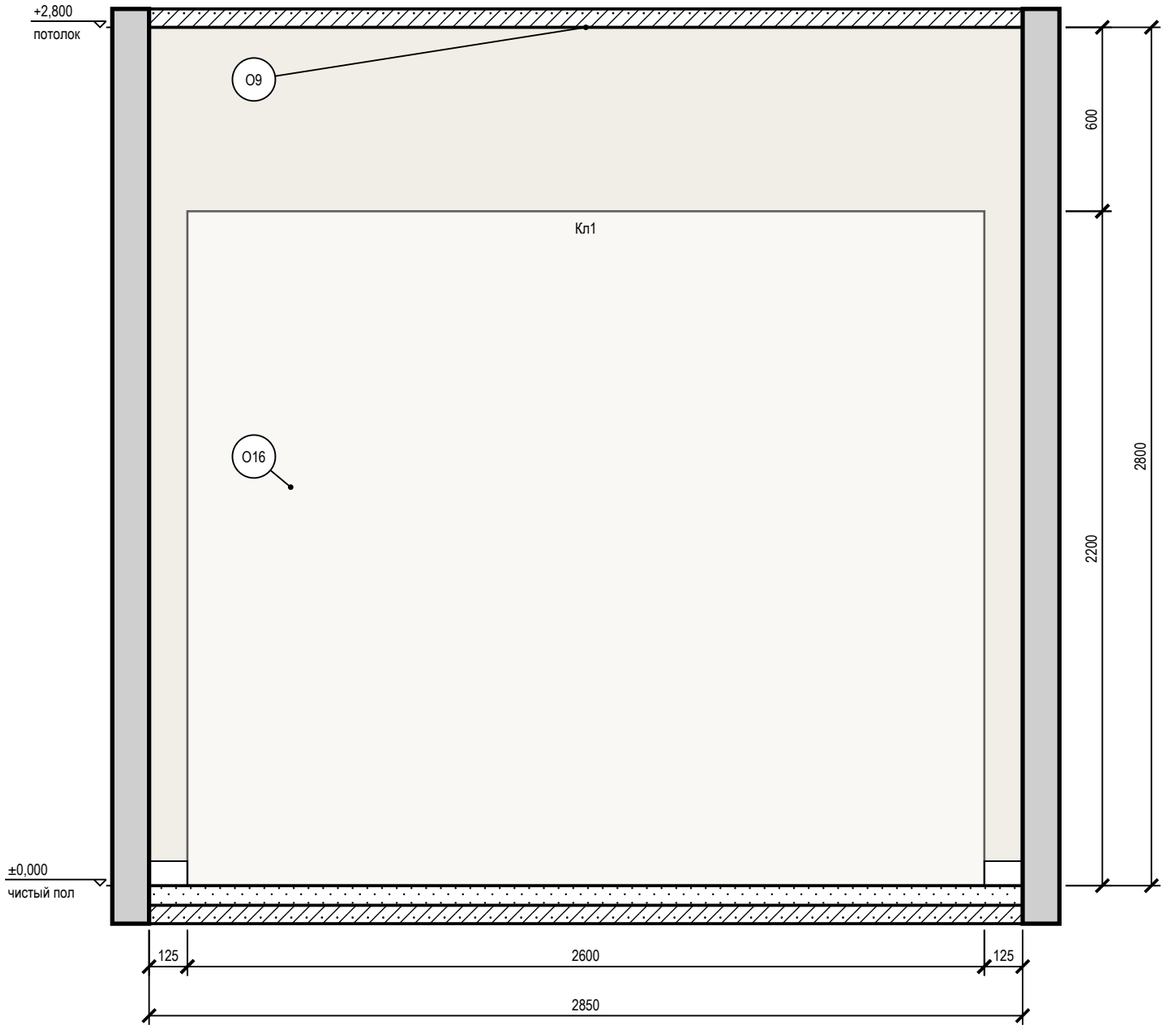

Схема развёрток (М 1:100)

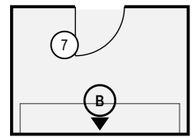

Условные обозначения

- привязки точек и выводов от угла и от пола, мм
- мебель и приборы — фасад по расстановке (условно)
- стены и перекрытия в сечении
- окраска: тон — цвет по коду производителя (условно)
- О1 — марка отделки по реестру отделки альбома
- А — марка развёртки: буква стены, стрелка — взгляд

Ведомость отделки (на листе)

Марка	Поверхность	Материал, изделие	Цвет, код	Кол.
О9	потолок	окраска, Tikkurila Anti-Reflex 2, глубокоматовая, подготовка Q3	Little Greene No. 105 «Slaked Lime»	6 м²
О16	стены	окраска, Tikkurila Harmony, матовая, подготовка Q3	Little Greene No. 105 «Slaked Lime»	8 м²
О17	плинтус	плинтус МДФ, h 80 мм, аналог: плинтус МДФ под покраску 80×16	Little Greene No. 105 «Slaked Lime»	0,3 м

Допущения и предложения на листе

Основа листа: размеры и контуры этажей подобраны проектировщиком по составу помещений и площадям этажей с картинки 470 px (размеры на ней не читаются); обмер и исходный проект — задание (К-1); высоты: 1-й этаж 2800 мм, мансарда 2700 мм (горизонтальная часть) приняты; скаты кровли мансарды приняты по картинке: колено 1200 мм, уклон 45°, конёк вдоль длинной стороны; проект КР — задание (К-2); наружные стены 400 мм, перегородки 120 мм приняты (К-1); разрешённая мощность 15 кВт принята по типовым ТУ для частного дома (К-4); подрайон климата не задан — принят не северный (жилые от 2,5 м) (К-7).

См. лист открытых вопросов (лист 7, записи К-1, К-2, К-4, К-7).

Примечания

1. Развёртки — вид на стену изнутри помещения, по часовой стрелке; расположение — на схеме листа и на листе 102; размеры — в мм по чистовым поверхностям; отметки — в м от ±0,000; высоты Н — от чистого пола помещения до оси изделия, у декора — до центра.
2. Красные цепочки — привязки электроточек и выводов: по горизонтали от угла чистовых стен, по вертикали от чистого пола, до оси изделия; звенья короче 3 мм на листе вынесены во второй ярус (ближняя к стене цепочка).
3. У знака электроточки: марка (Р — розетка, S — выключатель, Св — светильник, ЭВ — вывод кабеля), ×N — число постов в рамке, гр. — группа щита, Н — высота оси от чистого пола, мм; группы по клавишам выключателя — на листе выключателей.
4. Схема мебели, приборов и декора не является технической документацией для производства мебели; габариты — по паспортам изделий.

1000 мм · печать 1:1

Изм.	Кол.уч	Лист	№ док.	Подп.	Дата
Разраб.		Кырлан А.С.			21.10.26
Пров.					
ГИП					
Н. контр.					
Утв.					

ГД-2026-010-АИ

Дом 331 м²

Общая площадь 270,67* м² · * размеры приняты, не замерены (реестр — л. 7, К-1)

Дизайн-проект интерьера

Стадия	Лист	Листов
РП	117	159

Развёртки стен. Кладовая (пом. 7)

М 1:20

Кырлан Александр Сергеевич

выпуск 18.10.2026 № 9365d64cec · стр. 123 из 197

Развёртки стен А, Б. Прихожая (пом. 8)

Прихожая (пом. 8) · вид изнутри помещения · размеры в мм, отметки в м

ПРЕДВАРИТЕЛЬНО · не для производства работ · открыто пунктов: 6 (реестр — л. 7)

Развёртка стены А

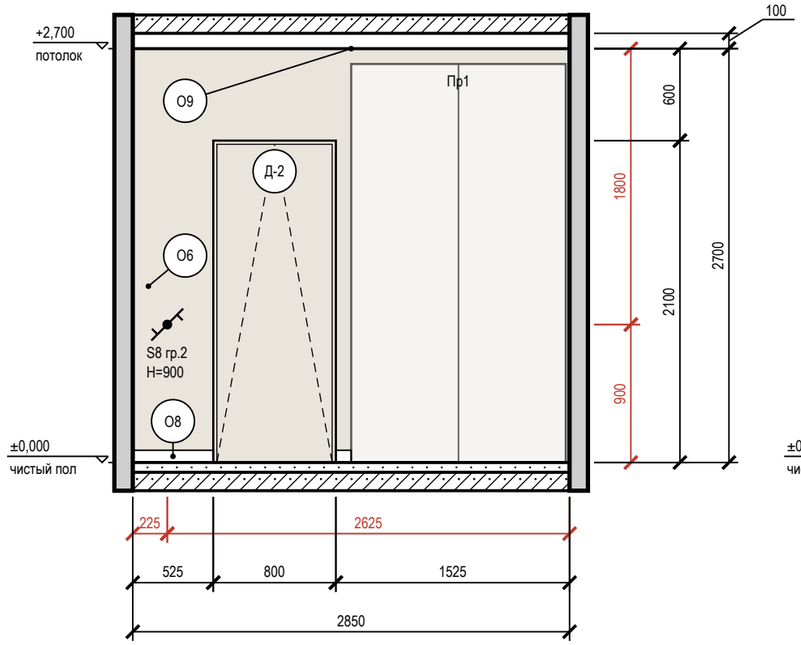

Развёртка стены Б

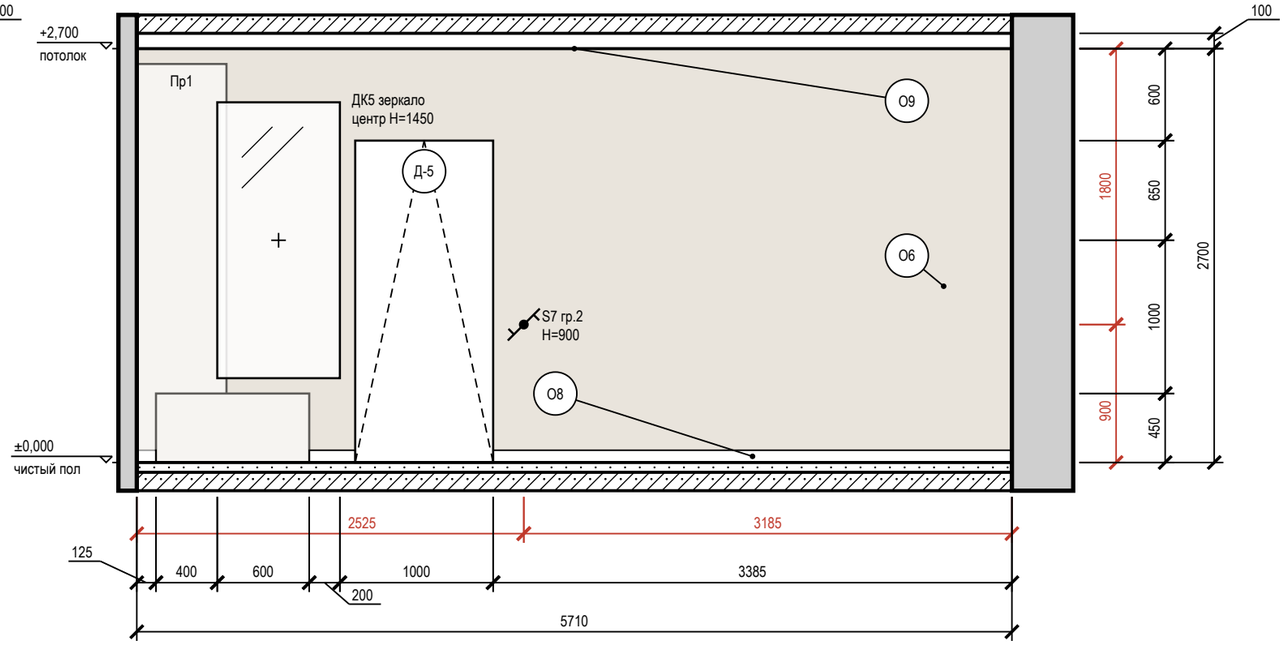

Схема развёрток (М 1:100)

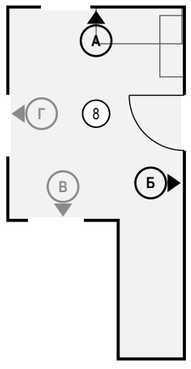

Условные обозначения

- выключатель одноклавишный
- выключатель с проходной или перекрёстной клавишей (обратный флажок); тип клавиши — в подписи
- привязки точек и выводов от угла и от пола, мм
- мебель и приборы — фасад по расстановке (условно)
- зеркало: марка Д, крест — центр, H — высота центра, мм
- дверь скрытого монтажа: полотно в плоскости стены (узел — на листе узлов)
- дверной проём; марка двери — в кружке
- стены и перекрытия в сечении
- окраска: тон — цвет по коду производителя (условно)
- О1 — марка отделки по реестру отделки альбома
- А — марка развёртки: буква стены, стрелка — взгляд

Ведомость отделки (на листе)

Марка	Поверхность	Материал, изделие	Цвет, код	Кол.
О6	стены	окраска, Farrow & Ball Modern Emulsion, матовая, подготовка Q3	Farrow & Ball No. 226 «Joa's White»	19,5 м²
О8	плинтус	плинтус МДФ, h 80 мм, аналог: плинтус МДФ под покраску 80×16	Farrow & Ball No. 226 «Joa's White»	4,4 м
О9	потолок	окраска, Tikkurila Anti-Reflex 2, глубокоматовая, подготовка Q3	Little Greene No. 105 «Slaked Lime»	12,5 м²

Допущения и предложения на листе

Основа листа: размеры и контуры этажей подобраны проектировщиком по составу помещений и площадям этажей с картинки 470 px (размеры на ней не читаются); обмер и исходный проект — задание (К-1); высоты: 1-й этаж 2800 мм, мансарда 2700 мм (горизонтальная часть) приняты; скаты кровли мансарды приняты по картинке: колено 1200 мм, уклон 45°, конёк вдоль длинной стороны; проект КР — задание (К-2); наружные стены 400 мм, перегородки 120 мм приняты (К-1); разрешённая мощность 15 кВт принята по типовым ТУ для частного дома (К-4); подрайон климата не задан — принят не северный (жилые от 2,5 м) (К-7).

См. лист открытых вопросов (лист 7, записи К-1, К-2, К-4, К-7).

Примечания

1. Развёртки — вид на стену изнутри помещения, по часовой стрелке; расположение — на схеме листа и на листе 102; размеры — в мм по чистовым поверхностям; отметки — в м от ±0,000; высоты H — от чистого пола помещения до оси изделия, у декора — до центра.
2. Красные цепочки — привязки электроточек и выводов: по горизонтали от угла чистовых стен, по вертикали от чистого пола, до оси изделия; звенья короче 3 мм на листе вынесены во второй ярус (ближняя к стене цепочка).
3. У знака электроточки: марка (Р — розетка, S — выключатель, Св — светильник, ЭВ — вывод кабеля), ×N — число постов в рамке, гр. — группа щита, H — высота оси от чистого пола, мм; группы по клавишам выключателя — на листе выключателей.
4. Схема мебели, приборов и декора не является технической документацией для производства мебели; габариты — по паспортам изделий.
5. Картины и зеркала крепить к основанию по паспорту изделия (закладные и анкеры — в перечне скрытых работ); крест — ось центра предмета.
6. Двери скрытого монтажа — полотно в плоскости стены, отделка стены по полотну, плинтус прерывается у короба (узел — на листе узлов).

1000 мм · печать 1:1

Изм.	Кол.уч	Лист	№ док.	Подп.	Дата
Разраб.		Кырлан А.С.			21.10.26
Пров.					
ГИП					
Н. контр.					
Утв.					

ГД-2026-010-АИ

Дом 331 м²

Общая площадь 270,67* м² · * размеры приняты, не замерены (реестр — л. 7, К-1)

Дизайн-проект интерьера

Стадия	Лист	Листов
РП	118	159

Развёртки стен А, Б. Прихожая (пом. 8)

М 1:40

Кырлан Александр Сергеевич

выпуск 18.10.2026 № 9365d64cec · стр. 124 из 197

Развёртки стен В, Г. Прихожая (пом. 8)

Прихожая (пом. 8) · вид изнутри помещения · размеры в мм, отметки в м

ПРЕДВАРИТЕЛЬНО · не для производства работ · открыто пунктов: 6 (реестр — л. 7)

Развёртка стены В

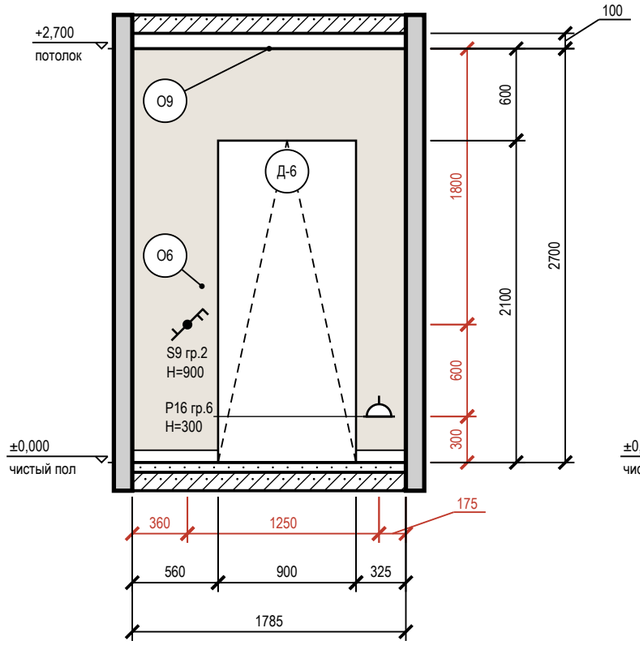

Развёртка стены Г

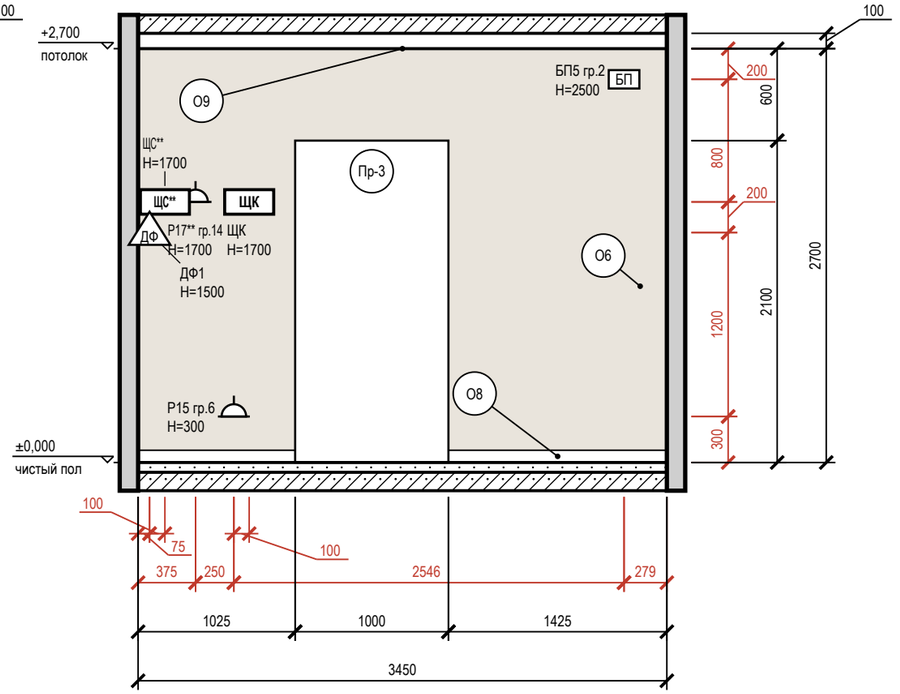

Условные обозначения

- розетка с заземляющим контактом; у знака — марка, ×N постов в рамке, гр. — группа щита, H — высота оси, мм
- выключатель одноклавишный
- выключатель двухклавишный (флажков — по числу клавиш)
- выключатель с проходной или перекрёстной клавишей (обратный флажок); тип клавиши — в подписи
- БП — блок питания LED, с доступом (люк от 100×100 мм)
- ДФ — трубка или монитор домофона
- ЩК — щит квартирный
- привязки точек и выводов от угла и от пола, мм
- мебель и приборы — фасад по расстановке (условно)
- дверной проём; марка двери — в кружке
- стены и перекрытия в сечении
- окраска: тон — цвет по коду производителя (условно)
- О1 — марка отделки по реестру отделки альбома
- А — марка развёртки: буква стены, стрелка — взгляд

Схема развёрток (М 1:100)

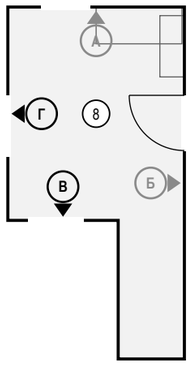

Ведомость отделки (на листе)

Марка	Поверхность	Материал, изделие	Цвет, код	Кол.
О6	стены	окраска, Farrow & Ball Modern Emulsion, матовая, подготовка Q3	Farrow & Ball No. 226 «Joa's White»	10,1 м²
О8	плинтус	плинтус МДФ, h 80 мм, аналог: плинтус МДФ под покраску 80×16	Farrow & Ball No. 226 «Joa's White»	3,3 м
О9	потолок	окраска, Tikkurila Anti-Reflex 2, глубокоматовая, подготовка Q3	Little Greene No. 105 «Slaked Lime»	12,5 м²

Допущения и предложения на листе

Основа листа: размеры и контуры этажей подобраны проектировщиком по составу помещений и площадям этажей с картинки 470 px (размеры на ней не читаются); обмер и исходный проект — задание (К-1); высоты: 1-й этаж 2800 мм, мансарда 2700 мм (горизонтальная часть) приняты; скаты кровли мансарды приняты по картинке: колено 1200 мм, уклон 45°, конёк вдоль длинной стороны; проект КР — задание (К-2); наружные стены 400 мм, перегородки 120 мм приняты (К-1); разрешённая мощность 15 кВт принята по типовым ТУ для частного дома (К-4); подрайон климата не задан — принят не северный (жилые от 2,5 м) (К-7).

Знак «**» — предложение проектировщика, заказчиком не утверждено (согласовать с заказчиком): записи в реестре нет: Р17 — высота 1700 мм выше нормы 1 м (ПУЭ 6.6.30) по назначению: питание слаботочного щита ЩС, рядом со щитом на его высоте; ЩС — щит слаботочный: место и состав.

См. лист открытых вопросов (лист 7, записи К-1, К-2, К-4, К-7).

Примечания

1. Развёртки — вид на стену изнутри помещения, по часовой стрелке; расположение — на схеме листа и на листе 102; размеры — в мм по чистовым поверхностям; отметки — в м от ±0,000; высоты H — от чистого пола помещения до оси изделия, у декора — до центра.
2. Красные цепочки — привязки электроточек и выводов: по горизонтали от угла чистовых стен, по вертикали от чистого пола, до оси изделия; звенья короче 3 мм на листе вынесены во второй ярус (ближняя к стене цепочка).
3. У знака электроточки: марка (Р — розетка, S — выключатель, Св — светильник, ЭВ — вывод кабеля), ×N — число постов в рамке, гр. — группа щита, H — высота оси от чистого пола, мм; группы по клавишам выключателя — на листе выключателей.
4. Схема мебели, приборов и декора не является технической документацией для производства мебели; габариты — по паспортам изделий.

1000 мм · печать 1:1

Изм.	Кол.уч	Лист	№ док.	Подп.	Дата
Разраб.		Кырлан А.С.			21.10.26
Пров.					
ГИП					
Н. контр.					
Утв.					

ГД-2026-010-АИ

Дом 331 м²

Общая площадь 270,67* м² · * размеры приняты, не замерены (реестр — л. 7, К-1)

Дизайн-проект интерьера

Стадия	Лист	Листов
РП	119	159

Развёртки стен В, Г. Прихожая (пом. 8)

М 1:40

Кырлан Александр Сергеевич

выпуск 18.10.2026 № 9365d64cec · стр. 125 из 197

Развёртки стен. Тамбур (пом. 9)

Тамбур (пом. 9) · вид изнутри помещения · размеры в мм, отметки в м

ПРЕДВАРИТЕЛЬНО · не для производства работ · открыто пунктов: 6 (реестр — л. 7)

Развёртка стены Г

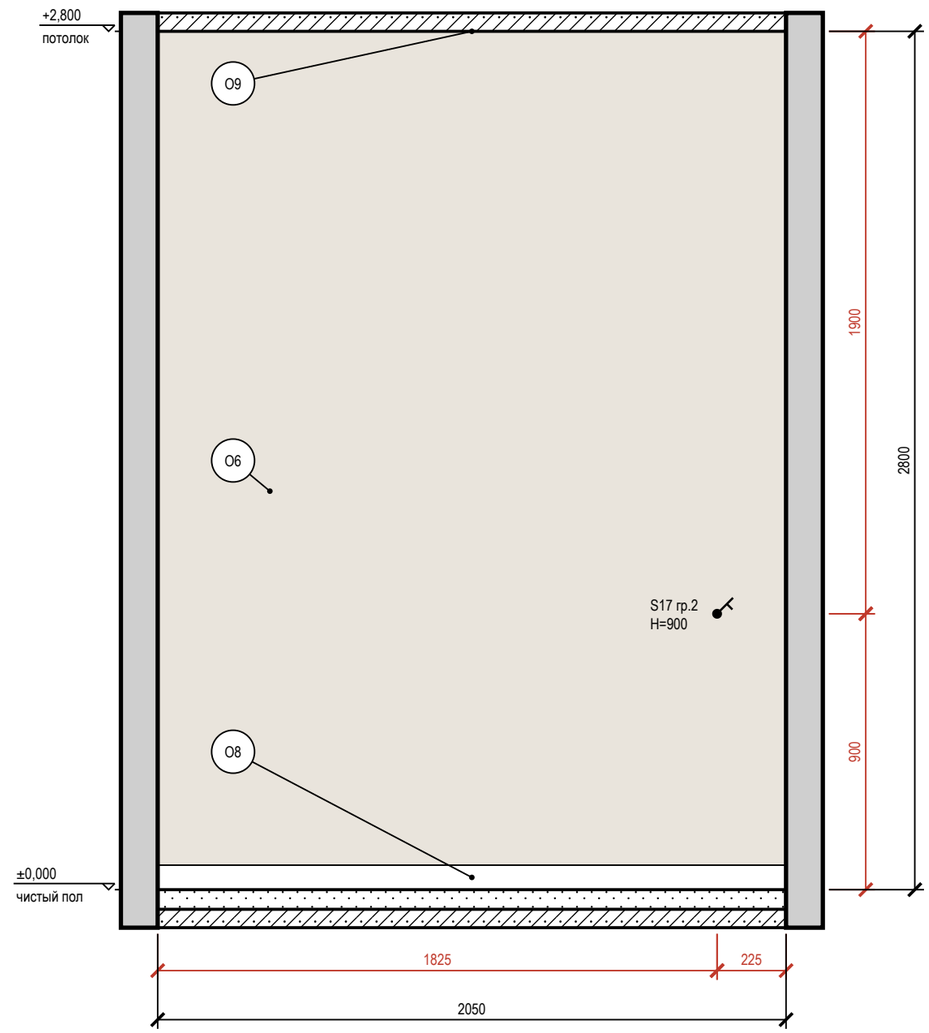

Схема развёрток (М 1:100)

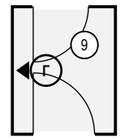

Условные обозначения

- выключатель одноклавишный
- привязки точек и выводов от угла и от пола, мм
- мебель и приборы — фасад по расстановке (условно)
- стены и перекрытия в сечении
- окраска: тон — цвет по коду производителя (условно)
- О1 — марка отделки по реестру отделки альбома
- А — марка развёртки: буква стены, стрелка — взгляд

Ведомость отделки (на листе)

Марка	Поверхность	Материал, изделие	Цвет, код	Кол.
О6	стены	окраска, Farrow & Ball Modern Emulsion, матовая, подготовка Q3	Farrow & Ball No. 226 «Joa's White»	5,7 м²
О8	плинтус	плинтус МДФ, h 80 мм, аналог: плинтус МДФ под покраску 80×16	Farrow & Ball No. 226 «Joa's White»	2 м
О9	потолок	окраска, Tikkurila Anti-Reflex 2, глубокоматовая, подготовка Q3	Little Greene No. 105 «Slaked Lime»	3,5 м²

Допущения и предложения на листе

Основа листа: размеры и контуры этажей подобраны проектировщиком по составу помещений и площадям этажей с картинки 470 px (размеры на ней не читаются); обмер и исходный проект — задание (К-1); высоты: 1-й этаж 2800 мм, мансарда 2700 мм (горизонтальная часть) приняты; скаты кровли мансарды приняты по картинке: колено 1200 мм, уклон 45°, конёк вдоль длинной стороны; проект КР — задание (К-2); наружные стены 400 мм, перегородки 120 мм приняты (К-1); разрешённая мощность 15 кВт принята по типовым ТУ для частного дома (К-4); подрайон климата не задан — принят не северный (жилые от 2,5 м) (К-7).

См. лист открытых вопросов (лист 7, записи К-1, К-2, К-4, К-7).

Примечания

1. Развёртки — вид на стену изнутри помещения, по часовой стрелке; расположение — на схеме листа и на листе 102; размеры — в мм по чистовым поверхностям; отметки — в м от ±0,000; высоты Н — от чистого пола помещения до оси изделия, у декора — до центра.
2. Красные цепочки — привязки электроточек и выводов: по горизонтали от угла чистовых стен, по вертикали от чистого пола, до оси изделия; звенья короче 3 мм на листе вынесены во второй ярус (ближняя к стене цепочка).
3. У знака электроточки: марка (Р — розетка, S — выключатель, Св — светильник, ЭВ — вывод кабеля), ×N — число постов в рамке, гр. — группа щита, Н — высота оси от чистого пола, мм; группы по клавишам выключателя — на листе выключателей.
4. Схема мебели, приборов и декора не является технической документацией для производства мебели; габариты — по паспортам изделий.

1000 мм · печать 1:1

Изм.	Кол.уч	Лист	№ док.	Подп.	Дата
Разраб.		Кырлан А.С.			21.10.26
Пров.					
ГИП					
Н. контр.					
Утв.					

ГД-2026-010-АИ

Дом 331 м²

Общая площадь 270,67* м² · * размеры приняты, не замерены (реестр — л. 7, К-1)

Дизайн-проект интерьера

Стадия	Лист	Листов
РП	120	159

Развёртки стен. Тамбур (пом. 9)

М 1:20

Кырлан Александр Сергеевич

выпуск 18.10.2026 № 9365d64cec · стр. 126 из 197

Развёртка стены А. Гараж (пом. 10)

Гараж (пом. 10) · вид изнутри помещения · размеры в мм, отметки в м

ПРЕДВАРИТЕЛЬНО · не для производства работ · открыто пунктов: 6 (реестр — л. 7)

Развёртка стены А

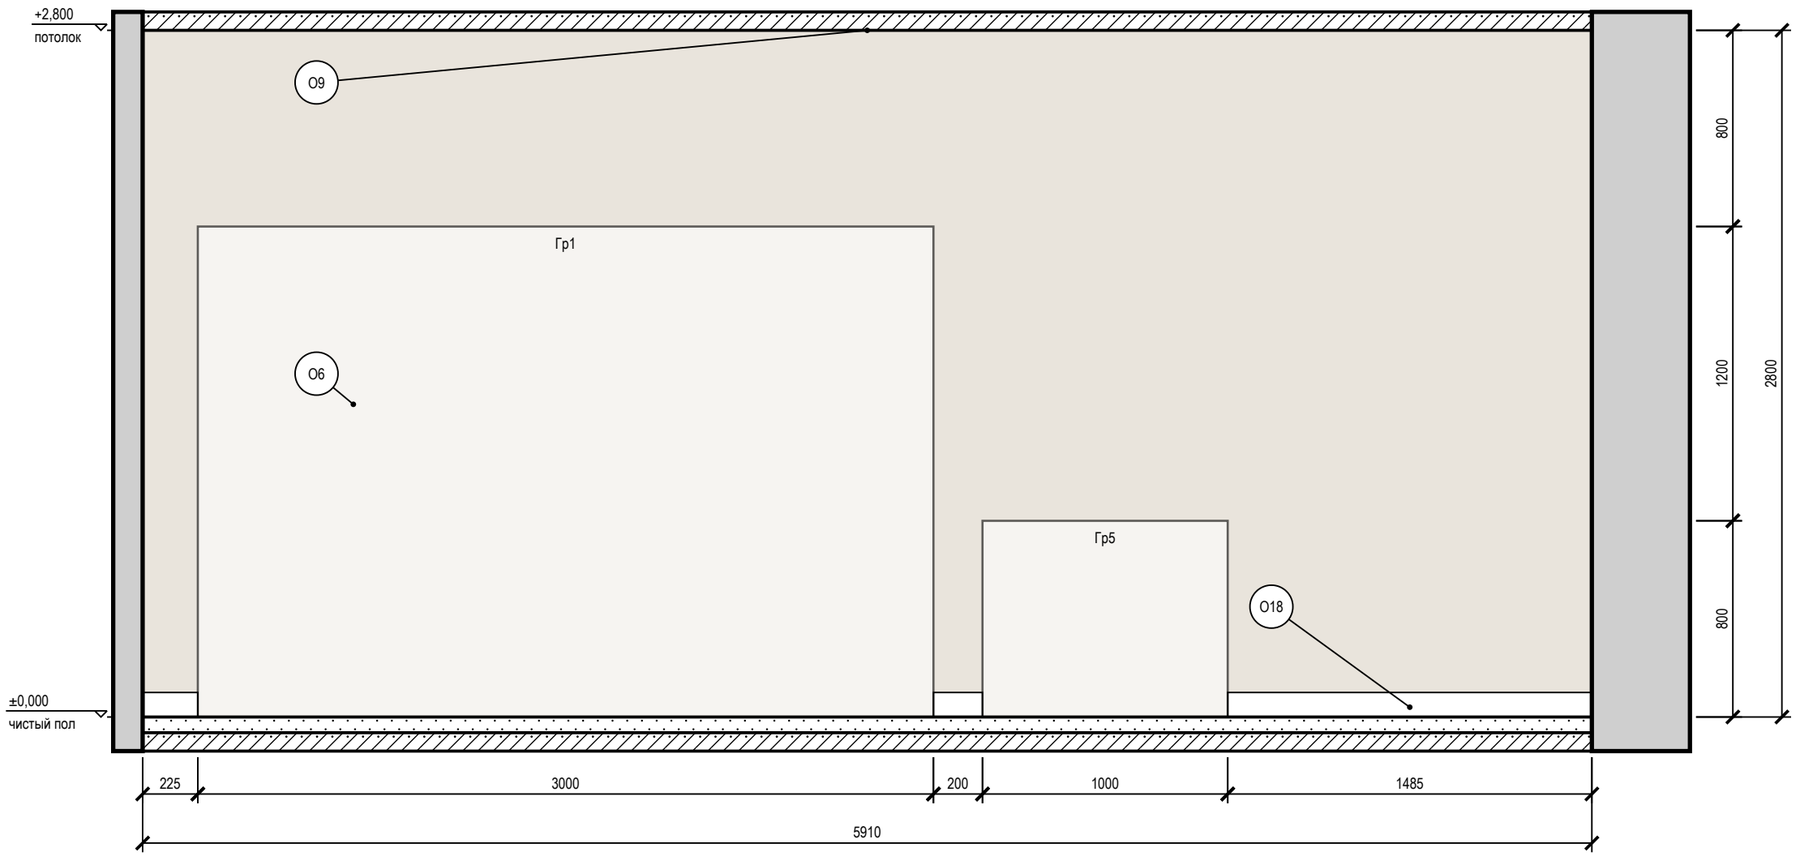

Схема развёрток (М 1:100)

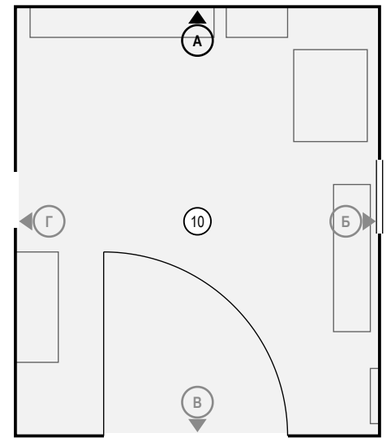

Условные обозначения

- привязки точек и выводов от угла и от пола, мм
- мебель и приборы — фасад по расстановке (условно)
- стены и перекрытия в сечении
- окраска: тон — цвет по коду производителя (условно)
- О1 — марка отделки по реестру отделки альбома
- А — марка развёртки: буква стены, стрелка — взгляд

Ведомость отделки (на листе)

Марка	Поверхность	Материал, изделие	Цвет, код	Кол.
О6	стены	окраска, Farrow & Ball Modern Emulsion, матовая, подготовка Q3	Farrow & Ball No. 226 «Joa's White»	16,5 м²
О9	потолок	окраска, Tikkurila Anti-Reflex 2, глубокоматовая, подготовка Q3	Little Greene No. 105 «Slaked Lime»	41,6 м²
О18	плинтус	плинтус ПВХ, h 100 мм, аналог: плинтус ПВХ влагостойкий 100 мм, серый		1,9 м

Допущения и предложения на листе

Основа листа: размеры и контуры этажей подобраны проектировщиком по составу помещений и площадям этажей с картинки 470 px (размеры на ней не читаются); обмер и исходный проект — задание (К-1); высоты: 1-й этаж 2800 мм, мансарда 2700 мм (горизонтальная часть) приняты; скаты кровли мансарды приняты по картинке: колено 1200 мм, уклон 45°, конёк вдоль длинной стороны; проект КР — задание (К-2); наружные стены 400 мм, перегородки 120 мм приняты (К-1); разрешённая мощность 15 кВт принята по типовым ТУ для частного дома (К-4); подрайон климата не задан — принят не северный (жилые от 2,5 м) (К-7).
См. лист открытых вопросов (лист 7, записи К-1, К-2, К-4, К-7).

Примечания

1. Развёртки — вид на стену изнутри помещения, по часовой стрелке; расположение — на схеме листа и на листе 102; размеры — в мм по чистовым поверхностям; отметки — в м от ±0,000; высоты Н — от чистого пола помещения до оси изделия, у декора — до центра.
2. Красные цепочки — привязки электроточек и выводов: по горизонтали от угла чистовых стен, по вертикали от чистого пола, до оси изделия; звенья короче 3 мм на листе вынесены во второй ярус (ближняя к стене цепочка).
3. У знака электроточки: марка (Р — розетка, S — выключатель, Св — светильник, ЭВ — вывод кабеля), ×N — число постов в рамке, гр. — группа щита, Н — высота оси от чистого пола, мм; группы по клавишам выключателя — на листе выключателей.
4. Схема мебели, приборов и декора не является технической документацией для производства мебели; габариты — по паспортам изделий.

1000 мм · печать 1:1

Изм.	Кол.уч	Лист	№ док.	Подп.	Дата
Разраб.		Кырлан А.С.			21.10.26
Пров.					
ГИП					
Н. контр.					
Утв.					

ГД-2026-010-АИ

Дом 331 м²

Общая площадь 270,67* м² · * размеры приняты, не замерены (реестр — л. 7, К-1)

Дизайн-проект интерьера

Стадия	Лист	Листов
РП	121	159

Развёртка стены А. Гараж (пом. 10)

М 1:25

Кырлан Александр Сергеевич

выпуск 18.10.2026 № 9365d64cec · стр. 127 из 197

Развёртка стены Б. Гараж (пом. 10)

Гараж (пом. 10) · вид изнутри помещения · размеры в мм, отметки в м

ПРЕДВАРИТЕЛЬНО · не для производства работ · открыто пунктов: 6 (реестр — л. 7)

Развёртка стены Б

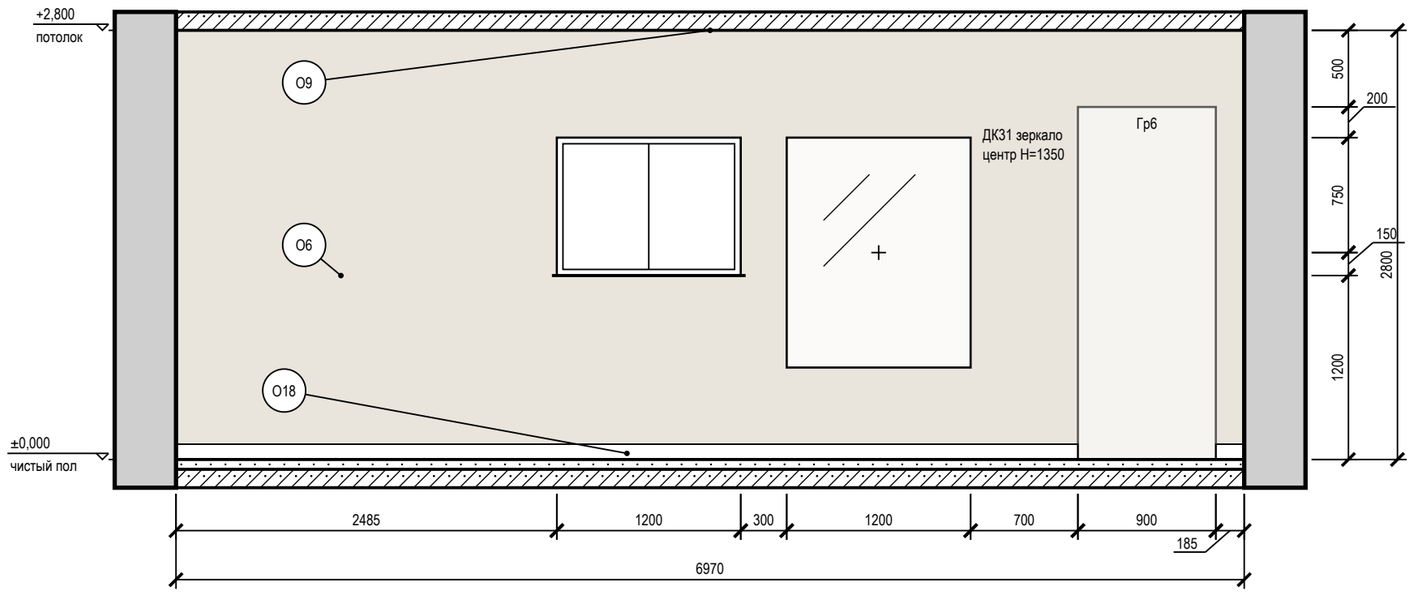

Условные обозначения

- привязки точек и выводов от угла и от пола, мм
- мебель и приборы — фасад по расстановке (условно)
- зеркало: марка Д, крест — центр, Н — высота центра, мм
- окно: проём, рама, подоконник
- стены и перекрытия в сечении
- окраска: тон — цвет по коду производителя (условно)
- О1 — марка отделки по реестру отделки альбома
- А — марка развёртки: буква стены, стрелка — взгляд

Схема развёрток (М 1:100)

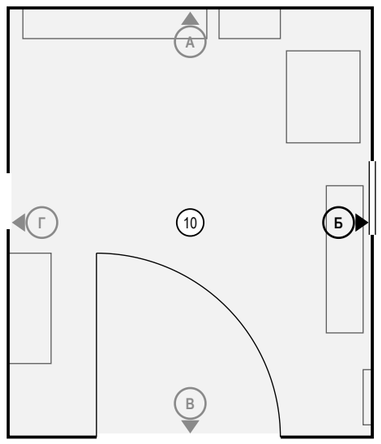

Ведомость отделки (на листе)

Марка	Поверхность	Материал, изделие	Цвет, код	Кол.
О6	стены	окраска, Farrow & Ball Modern Emulsion, матовая, подготовка Q3	Farrow & Ball No. 226 «Joa's White»	18,4 м²
О9	потолок	окраска, Tikkurila Anti-Reflex 2, глубокоматовая, подготовка Q3	Little Greene No. 105 «Slaked Lime»	41,6 м²
О18	плинтус	плинтус ПВХ, h 100 мм, аналог: плинтус ПВХ влагостойкий 100 мм, серый		6,1 м

Допущения и предложения на листе

Основа листа: размеры и контуры этажей подобраны проектировщиком по составу помещений и площадям этажей с картинки 470 px (размеры на ней не читаются); обмер и исходный проект — задание (К-1); высоты: 1-й этаж 2800 мм, мансарда 2700 мм (горизонтальная часть) приняты; скаты кровли мансарды приняты по картинке: колено 1200 мм, уклон 45°, конёк вдоль длинной стороны; проект КР — задание (К-2); наружные стены 400 мм, перегородки 120 мм приняты (К-1); разрешённая мощность 15 кВт принята по типовым ТУ для частного дома (К-4); подрайон климата не задан — принят не северный (жилые от 2,5 м) (К-7).

См. лист открытых вопросов (лист 7, записи К-1, К-2, К-4, К-7).

Примечания

1. Развёртки — вид на стену изнутри помещения, по часовой стрелке; расположение — на схеме листа и на листе 102; размеры — в мм по чистовым поверхностям; отметки — в м от ±0,000; высоты Н — от чистого пола помещения до оси изделия, у декора — до центра.
2. Красные цепочки — привязки электроточек и выводов: по горизонтали от угла чистовых стен, по вертикали от чистого пола, до оси изделия; звенья короче 3 мм на листе вынесены во второй ярус (ближняя к стене цепочка).
3. У знака электроточки: марка (Р — розетка, S — выключатель, Св — светильник, ЭВ — вывод кабеля), ×N — число постов в рамке, гр. — группа щита, Н — высота оси от чистого пола, мм; группы по клавишам выключателя — на листе выключателей.
4. Схема мебели, приборов и декора не является технической документацией для производства мебели; габариты — по паспортам изделий.
5. Картины и зеркала крепить к основанию по паспорту изделия (закладные и анкеры — в перечне скрытых работ); крест — ось центра предмета.

1000 мм · печать 1:1

Изм.	Кол.уч	Лист	№ док.	Подп.	Дата
Разраб.		Кырлан А.С.			21.10.26
Пров.					
ГИП					
Н. контр.					
Утв.					

ГД-2026-010-АИ

Дом 331 м²

Общая площадь 270,67* м² · * размеры приняты, не замерены (реестр — л. 7, К-1)

Дизайн-проект интерьера

Стадия	Лист	Листов
РП	122	159

Развёртка стены Б. Гараж (пом. 10)

М 1:40

Кырлан Александр Сергеевич

выпуск 18.10.2026 № 9365d64cec · стр. 128 из 197

Развёртка стены В. Гараж (пом. 10)

Гараж (пом. 10) · вид изнутри помещения · размеры в мм, отметки в м

ПРЕДВАРИТЕЛЬНО · не для производства работ · открыто пунктов: 6 (реестр — л. 7)

Развёртка стены В

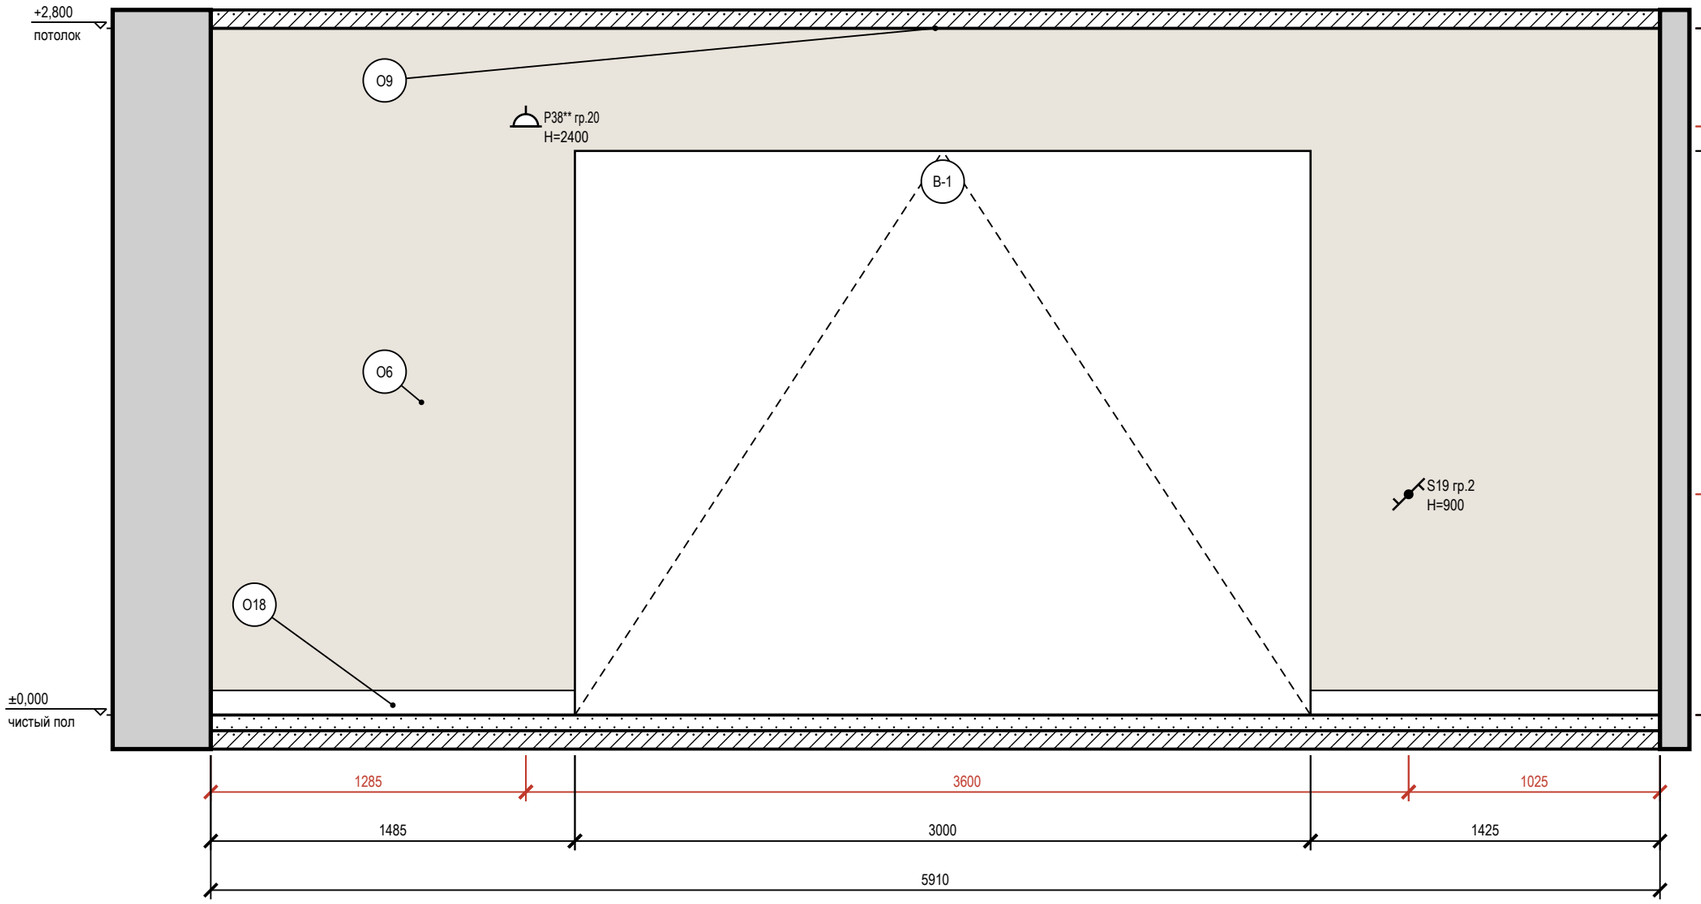

Схема развёрток (М 1:100)

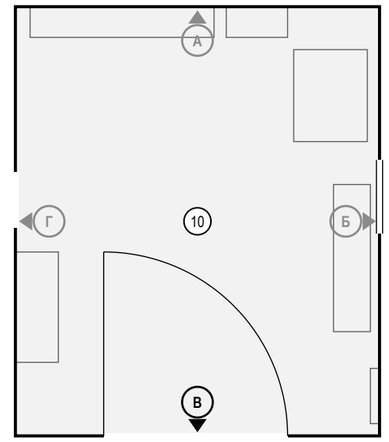

Допущения и предложения на листе

Основа листа: размеры и контуры этажей подобраны проектировщиком по составу помещений и площадям этажей с картинки 470 px (размеры на ней не читаются); обмер и исходный проект — задание (К-1); высоты: 1-й этаж 2800 мм, мансарда 2700 мм (горизонтальная часть) приняты; скаты кровли мансарды приняты по картинке: колено 1200 мм, уклон 45°, конёк вдоль длинной стороны; проект КР — задание (К-2); наружные стены 400 мм, перегородки 120 мм приняты (К-1); разрешённая мощность 15 кВт принята по типовым ТУ для частного дома (К-4); подрайон климата не задан — принят не северный (жилые от 2,5 м) (К-7).

Знак «**» — предложение проектировщика, заказчиком не утверждено (согласовать с заказчиком): записи в реестре нет: Р38 — высота 2400 мм выше 1 м по назначению: питание привода ворот у его места на потолке.

См. лист открытых вопросов (лист 7, записи К-1, К-2, К-4, К-7).

Условные обозначения

- розетка с заземляющим контактом; у знака — марка, ×N постов в рамке, гр. — группа щита, H — высота оси, мм
- выключатель одноклавишный
- выключатель с проходной или перекрёстной клавишей (обратный флажок); тип клавиши — в подписи
- привязки точек и выводов от угла и от пола, мм
- мебель и приборы — фасад по расстановке (условно)
- дверной проём; марка двери — в кружке
- стены и перекрытия в сечении
- окраска: тон — цвет по коду производителя (условно)
- О1 — марка отделки по реестру отделки альбома
- А — марка развёртки: буква стены, стрелка — взгляд

Ведомость отделки (на листе)

Марка	Поверхность	Материал, изделие	Цвет, код	Кол.
О6	стены	окраска, Farrow & Ball Modern Emulsion, матовая, подготовка Q3	Farrow & Ball No. 226 «Joa's White»	9,6 м²
О9	потолок	окраска, Tikkurila Anti-Reflex 2, глубокоматовая, подготовка Q3	Little Greene No. 105 «Slaked Lime»	41,6 м²
О18	плинтус	плинтус ПВХ, h 100 мм, аналог: плинтус ПВХ влагостойкий 100 мм, серый		2,9 м

Примечания

1. Развёртки — вид на стену изнутри помещения, по часовой стрелке; расположение — на схеме листа и на листе 102; размеры — в мм по чистовым поверхностям; отметки — в м от ±0,000; высоты H — от чистого пола помещения до оси изделия, у декора — до центра.
2. Красные цепочки — привязки электроточек и выводов: по горизонтали от угла чистовых стен, по вертикали от чистого пола, до оси изделия; звенья короче 3 мм на листе вынесены во второй ярус (ближняя к стене цепочка).
3. У знака электроточки: марка (Р — розетка, S — выключатель, Св — светильник, ЭВ — вывод кабеля), ×N — число постов в рамке, гр. — группа щита, H — высота оси от чистого пола, мм; группы по клавишам выключателя — на листе выключателей.
4. Схема мебели, приборов и декора не является технической документацией для производства мебели; габариты — по паспортам изделий.

1000 мм · печать 1:1

Изм.	Кол.уч	Лист	№ док.	Подп.	Дата
Разраб.		Кырлан А.С.			21.10.26
Пров.					
ГИП					
Н. контр.					
Утв.					

ГД-2026-010-АИ

Дом 331 м²

Общая площадь 270,67* м² · * размеры приняты, не замерены (реестр — л. 7, К-1)

Дизайн-проект интерьера

Стадия	Лист	Листов
РП	123	159

Развёртка стены В. Гараж (пом. 10)

М 1:25

Кырлан Александр Сергеевич

выпуск 18.10.2026 № 9365d64cec · стр. 129 из 197

Развёртка стены Г. Гараж (пом. 10)

Гараж (пом. 10) · вид изнутри помещения · размеры в мм, отметки в м

ПРЕДВАРИТЕЛЬНО · не для производства работ · открыто пунктов: 6 (реестр — л. 7)

Развёртка стены Г

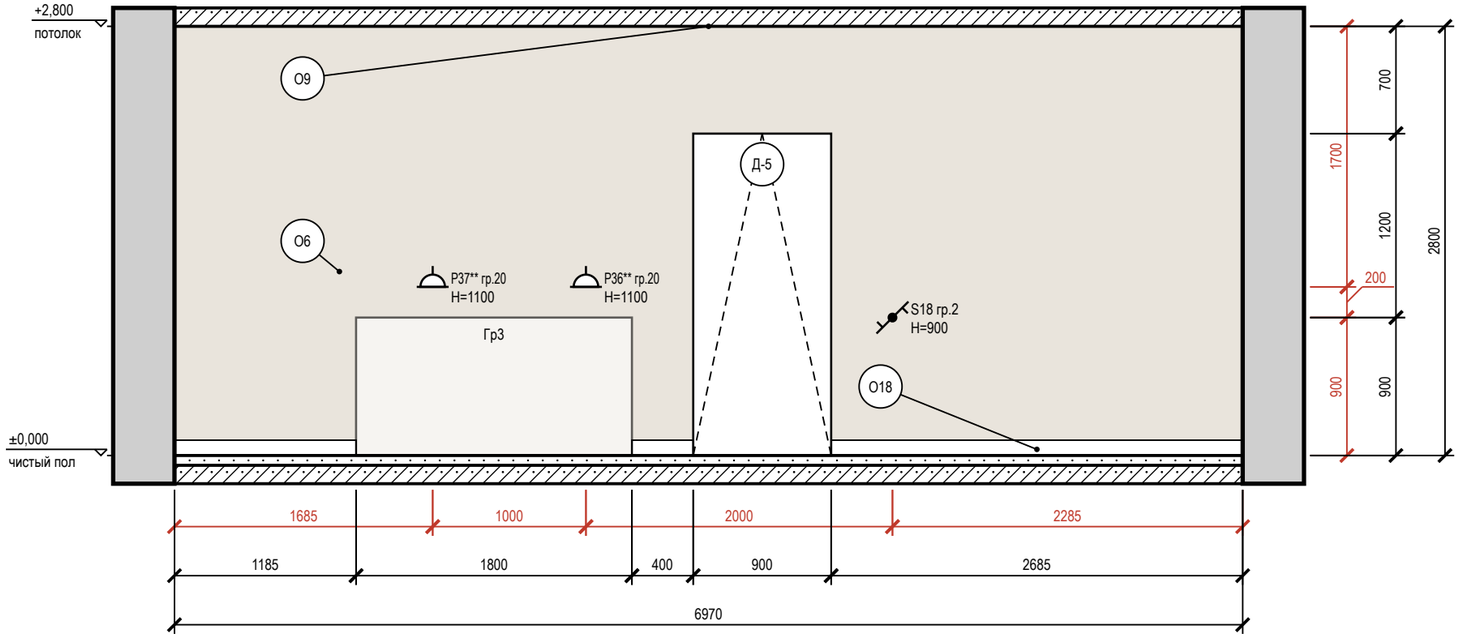

Схема развёрток (М 1:100)

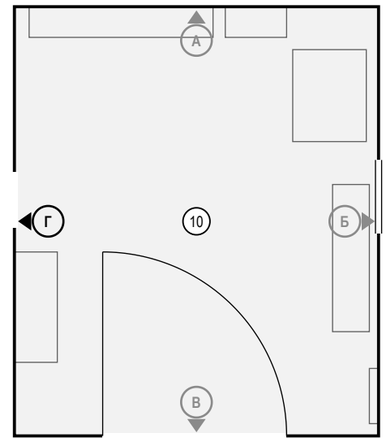

Ведомость отделки (на листе)

Марка	Поверхность	Материал, изделие	Цвет, код	Кол.
О6	стены	окраска, Farrow & Ball Modern Emulsion, матовая, подготовка Q3	Farrow & Ball No. 226 «Joa's White»	17,6 м²
О9	потолок	окраска, Tikkurila Anti-Reflex 2, глубокоматовая, подготовка Q3	Little Greene No. 105 «Slaked Lime»	41,6 м²
О18	плинтус	плинтус ПВХ, h 100 мм, аналог: плинтус ПВХ влагостойкий 100 мм, серый		4,3 м

Условные обозначения

- розетка с заземляющим контактом; у знака — марка, ×N постов в рамке, гр. — группа щита, Н — высота оси, мм
- выключатель одноклавишный
- выключатель с проходной или перекрёстной клавишей (обратный флажок); тип клавиши — в подписи
- привязки точек и выводов от угла и от пола, мм
- мебель и приборы — фасад по расстановке (условно)
- дверной проём; марка двери — в кружке
- стены и перекрытия в сечении
- окраска: тон — цвет по коду производителя (условно)
- О1 — марка отделки по реестру отделки альбома
- А — марка развёртки: буква стены, стрелка — взгляд

Допущения и предложения на листе

Основа листа: размеры и контуры этажей подобраны проектировщиком по составу помещений и площадям этажей с картинки 470 px (размеры на ней не читаются); обмер и исходный проект — задание (К-1); высоты: 1-й этаж 2800 мм, мансарда 2700 мм (горизонтальная часть) приняты; скаты кровли мансарды приняты по картинке: колено 1200 мм, уклон 45°, конёк вдоль длинной стороны; проект КР — задание (К-2); наружные стены 400 мм, перегородки 120 мм приняты (К-1); разрешённая мощность 15 кВт принята по типовым ТУ для частного дома (К-4); подрайон климата не задан — принят не северный (жилые от 2,5 м) (К-7).

Знак «**» — предложение проектировщика, заказчиком не утверждено (согласовать с заказчиком): записи в реестре нет: Р36, Р37 — высота 1100 мм выше 1 м по назначению: над столешницей верстака 900 мм.

См. лист открытых вопросов (лист 7, записи К-1, К-2, К-4, К-7).

Примечания

1. Развёртки — вид на стену изнутри помещения, по часовой стрелке; расположение — на схеме листа и на листе 102; размеры — в мм по чистовым поверхностям; отметки — в м от ±0,000; высоты Н — от чистого пола помещения до оси изделия, у декора — до центра.
2. Красные цепочки — привязки электроточек и выводов: по горизонтали от угла чистовых стен, по вертикали от чистого пола, до оси изделия; звенья короче 3 мм на листе вынесены во второй ярус (ближняя к стене цепочка).
3. У знака электроточки: марка (Р — розетка, S — выключатель, Св — светильник, ЭВ — вывод кабеля), ×N — число постов в рамке, гр. — группа щита, Н — высота оси от чистого пола, мм; группы по клавишам выключателя — на листе выключателей.
4. Схема мебели, приборов и декора не является технической документацией для производства мебели; габариты — по паспортам изделий.

1000 мм · печать 1:1

Изм.	Кол.уч	Лист	№ док.	Подп.	Дата
Разраб.		Кырлан А.С.			21.10.26
Пров.					
ГИП					
Н. контр.					
Утв.					

ГД-2026-010-АИ

Дом 331 м²

Общая площадь 270,67* м² · * размеры приняты, не замерены (реестр — л. 7, К-1)

Дизайн-проект интерьера

Стадия	Лист	Листов
РП	124	159

Развёртка стены Г. Гараж (пом. 10)

М 1:40

Кырлан Александр Сергеевич

выпуск 18.10.2026 № 9365d64cec · стр. 130 из 197

Развёртка стены А. Веранда (пом. 11)

Веранда (пом. 11) · вид изнутри помещения · размеры в мм, отметки в м

ПРЕДВАРИТЕЛЬНО · не для производства работ · открыто пунктов: 6 (реестр — л. 7)

Развёртка стены А

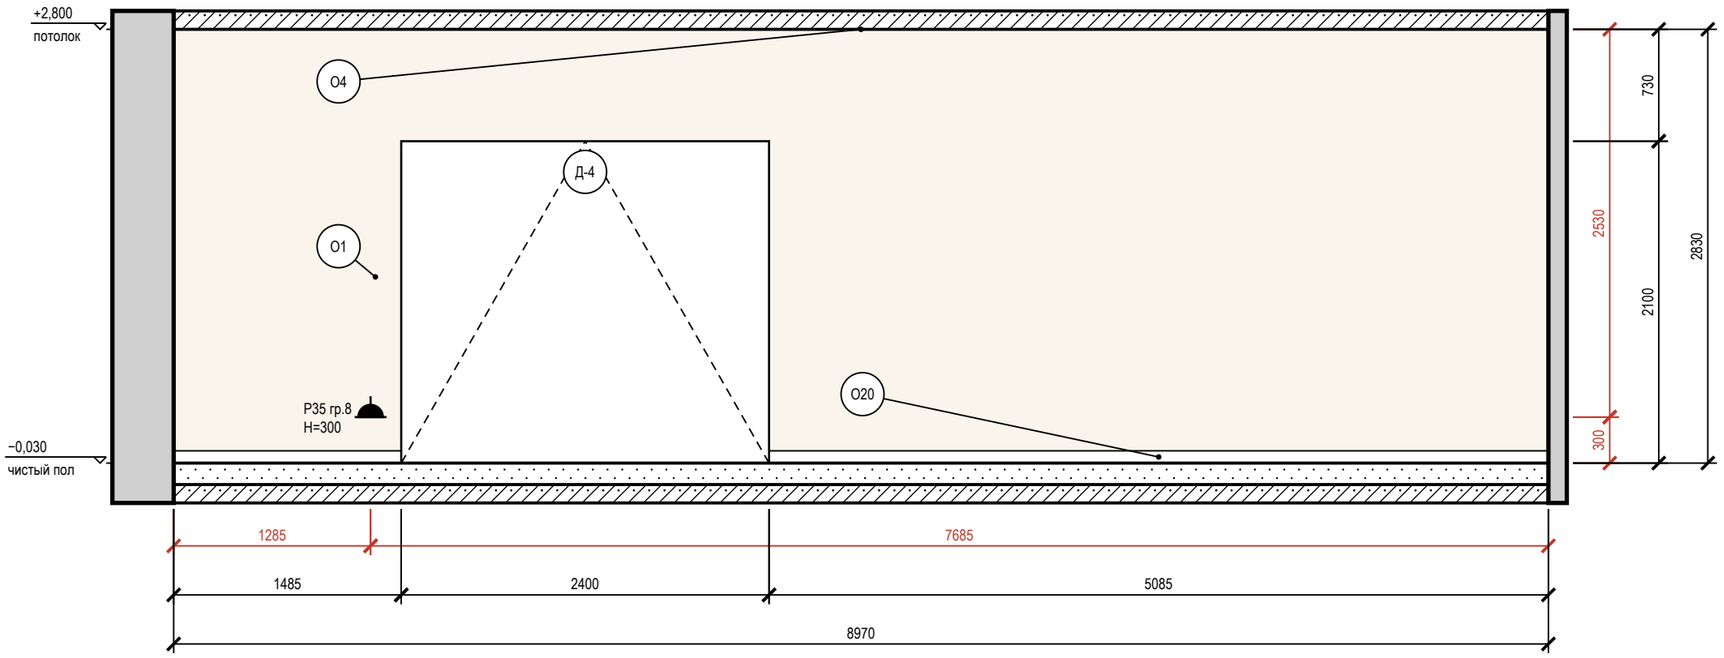

Условные обозначения

- розетка влагозащищённая IP44
- привязки точек и выводов от угла и от пола, мм
- мебель и приборы — фасад по расстановке (условно)
- дверной проём; марка двери — в кружке
- стены и перекрытия в сечении
- окраска: тон — цвет по коду производителя (условно)
- О1 — марка отделки по реестру отделки альбома
- А — марка развёртки: буква стены, стрелка — взгляд

Схема развёрток (М 1:100)

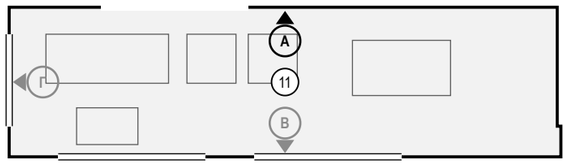

Ведомость отделки (на листе)

Марка	Поверхность	Материал, изделие	Цвет, код	Кол.
О1	стены	окраска, Tikkurila Luja 7, шелковисто-матовая, подготовка К3	NCS S 0804-Y30R «S 0804-Y30R»	20,3 м²
О4	потолок	окраска, Tikkurila Luja 7, матовая, подготовка Q3	NCS S 0804-Y30R «S 0804-Y30R»	21,8 м²
О20	плинтус	керамогранит, аналог: плинтус из керамогранита пола, подрезка 80 мм, верхняя кромка с запилом 45°	#B8AFA5 «тон Claystone V486»	6,6 м

Допущения и предложения на листе

Основа листа: размеры и контуры этажей подобраны проектировщиком по составу помещений и площадям этажей с картинки 470 px (размеры на ней не читаются); обмер и исходный проект — задание (К-1); высоты: 1-й этаж 2800 мм, мансарда 2700 мм (горизонтальная часть) приняты; скаты кровли мансарды приняты по картинке: колено 1200 мм, уклон 45°, конёк вдоль длинной стороны; проект КР — задание (К-2); наружные стены 400 мм, перегородки 120 мм приняты (К-1); разрешённая мощность 15 кВт принята по типовым ТУ для частного дома (К-4); подрайон климата не задан — принят не северный (жилые от 2,5 м) (К-7).

См. лист открытых вопросов (лист 7, записи К-1, К-2, К-4, К-7).

Примечания

1. Развёртки — вид на стену изнутри помещения, по часовой стрелке; расположение — на схеме листа и на листе 102; размеры — в мм по чистовым поверхностям; отметки — в м от ±0,000; высоты Н — от чистого пола помещения до оси изделия, у декора — до центра.
2. Красные цепочки — привязки электроточек и выводов: по горизонтали от угла чистовых стен, по вертикали от чистого пола, до оси изделия; звенья короче 3 мм на листе вынесены во второй ярус (ближняя к стене цепочка).
3. У знака электроточки: марка (Р — розетка, S — выключатель, Св — светильник, ЭВ — вывод кабеля), ×N — число постов в рамке, гр. — группа щита, Н — высота оси от чистого пола, мм; группы по клавишам выключателя — на листе выключателей.
4. Схема мебели, приборов и декора не является технической документацией для производства мебели; габариты — по паспортам изделий.

1000 мм · печать 1:1

Изм.	Кол.уч	Лист	№ док.	Подп.	Дата
Разраб.		Кырлан А.С.			21.10.26
Пров.					
ГИП					
Н. контр.					
Утв.					

ГД-2026-010-АИ

Дом 331 м²

Общая площадь 270,67* м² · * размеры приняты, не замерены (реестр — л. 7, К-1)

Дизайн-проект интерьера

Стадия	Лист	Листов
РП	125	159

Развёртка стены А. Веранда (пом. 11)

М 1:40

Кырлан Александр Сергеевич

выпуск 18.10.2026 № 9365d64cec · стр. 131 из 197

Развёртка стены В. Веранда (пом. 11)

Веранда (пом. 11) · вид изнутри помещения · размеры в мм, отметки в м

ПРЕДВАРИТЕЛЬНО · не для производства работ · открыто пунктов: 6 (реестр — л. 7)

Развёртка стены В

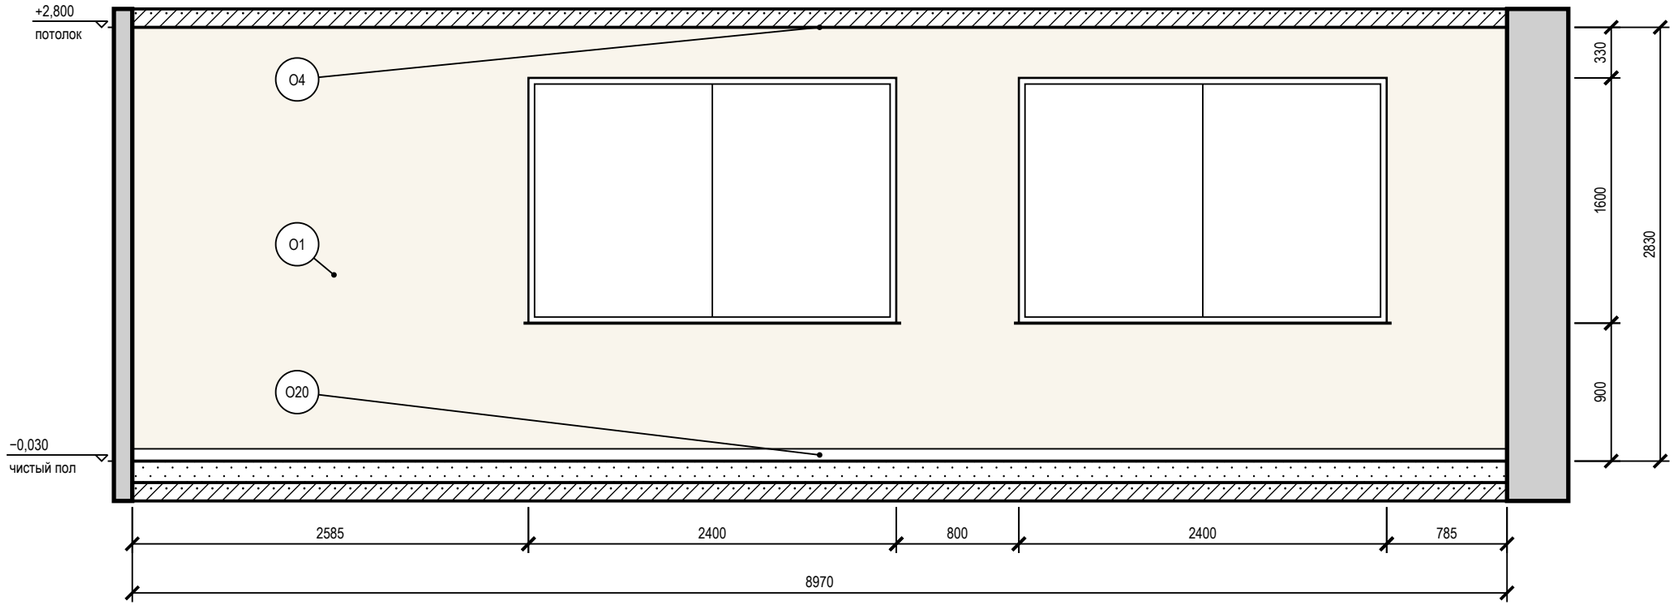

Условные обозначения

- привязки точек и выводов от угла и от пола, мм
- мебель и приборы — фасад по расстановке (условно)
- окно: проём, рама, подоконник
- стены и перекрытия в сечении
- окраска: тон — цвет по коду производителя (условно)
- О1 — марка отделки по реестру отделки альбома
- А — марка развёртки: буква стены, стрелка — взгляд

Схема развёрток (М 1:100)

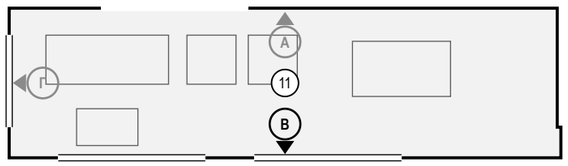

Ведомость отделки (на листе)

Марка	Поверхность	Материал, изделие	Цвет, код	Кол.
О1	стены	окраска, Tikkurila Luja 7, шелковисто-матовая, подготовка К3	NCS S 0804-Y30R «S 0804-Y30R»	17,7 м²
О4	потолок	окраска, Tikkurila Luja 7, матовая, подготовка Q3	NCS S 0804-Y30R «S 0804-Y30R»	21,8 м²
О20	плинтус	керамогранит, аналог: плинтус из керамогранита пола, подрезка 80 мм, верхняя кромка с запилом 45°	#B8AFA5 «тон Claystone V486»	9 м

Допущения и предложения на листе

Основа листа: размеры и контуры этажей подобраны проектировщиком по составу помещений и площадям этажей с картинки 470 px (размеры на ней не читаются); обмер и исходный проект — задание (К-1); высоты: 1-й этаж 2800 мм, мансарда 2700 мм (горизонтальная часть) приняты; скаты кровли мансарды приняты по картинке: колено 1200 мм, уклон 45°, конёк вдоль длинной стороны; проект КР — задание (К-2); наружные стены 400 мм, перегородки 120 мм приняты (К-1); разрешённая мощность 15 кВт принята по типовым ТУ для частного дома (К-4); подрайон климата не задан — принят не северный (жилые от 2,5 м) (К-7).

См. лист открытых вопросов (лист 7, записи К-1, К-2, К-4, К-7).

Примечания

1. Развёртки — вид на стену изнутри помещения, по часовой стрелке; расположение — на схеме листа и на листе 102; размеры — в мм по чистовым поверхностям; отметки — в м от ±0,000; высоты Н — от чистого пола помещения до оси изделия, у декора — до центра.
2. Красные цепочки — привязки электроточек и выводов: по горизонтали от угла чистовых стен, по вертикали от чистого пола, до оси изделия; звенья короче 3 мм на листе вынесены во второй ярус (ближняя к стене цепочка).
3. У знака электроточки: марка (Р — розетка, S — выключатель, Св — светильник, ЭВ — вывод кабеля), ×N — число постов в рамке, гр. — группа щита, Н — высота оси от чистого пола, мм; группы по клавишам выключателя — на листе выключателей.
4. Схема мебели, приборов и декора не является технической документацией для производства мебели; габариты — по паспортам изделий.

1000 мм · печать 1:1

Изм.	Кол.уч	Лист	№ док.	Подп.	Дата
Разраб.		Кырлан А.С.			21.10.26
Пров.					
ГИП					
Н. контр.					
Утв.					

ГД-2026-010-АИ

Дом 331 м²

Общая площадь 270,67* м² · * размеры приняты, не замерены (реестр — л. 7, К-1)

Дизайн-проект интерьера

Стадия	Лист	Листов
РП	126	159

Развёртка стены В. Веранда (пом. 11)

М 1:40

Кырлан Александр Сергеевич

выпуск 18.10.2026 № 9365d64cec · стр. 132 из 197

Развёртка стены Г. Веранда (пом. 11)

Веранда (пом. 11) · вид изнутри помещения · размеры в мм, отметки в м

ПРЕДВАРИТЕЛЬНО · не для производства работ · открыто пунктов: 6 (реестр — л. 7)

Развёртка стены Г

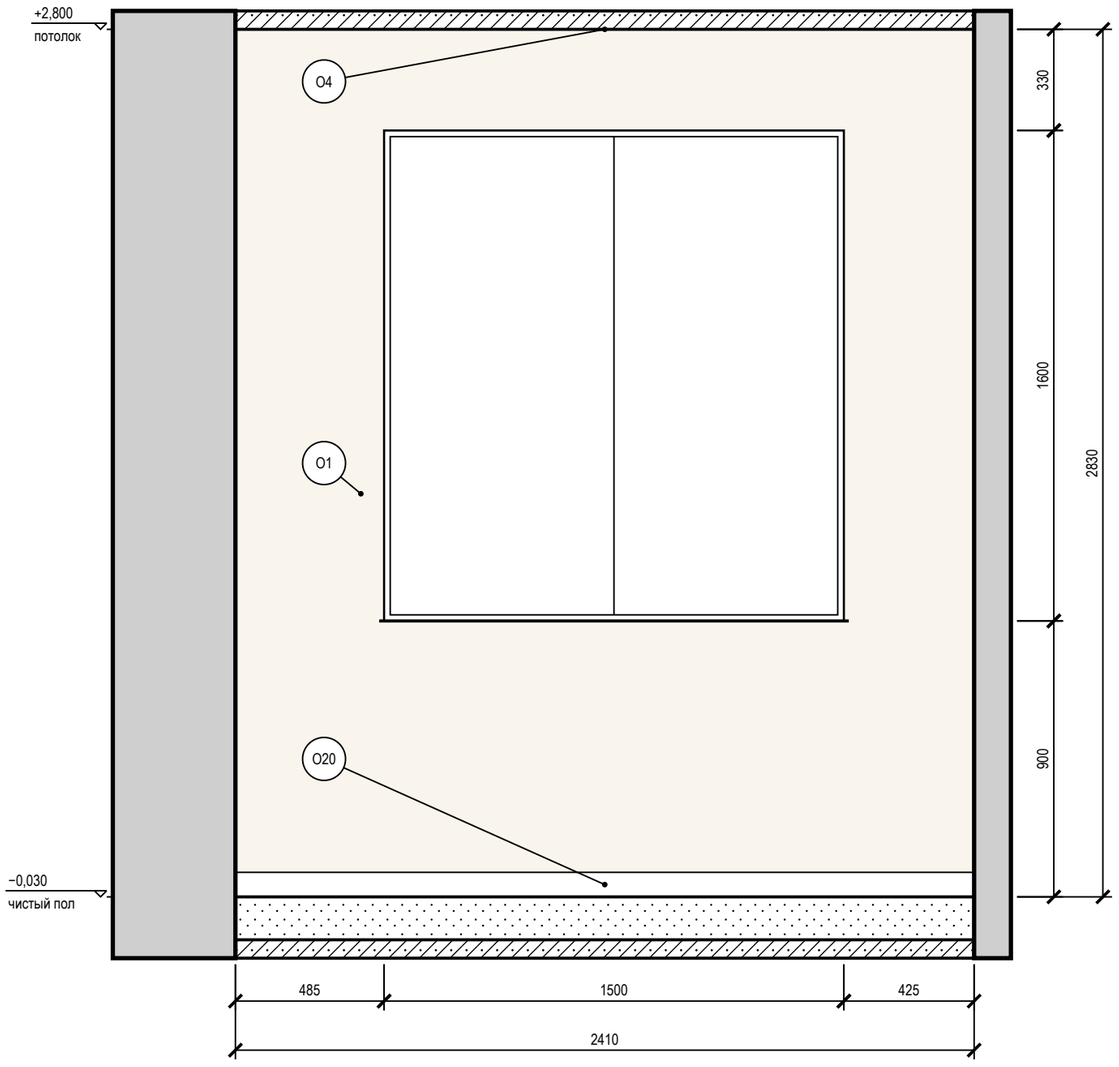

Схема развёрток (М 1:100)

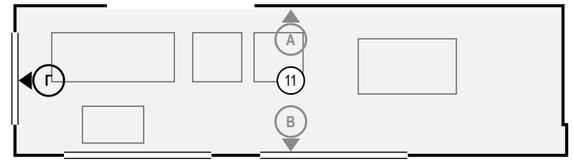

Условные обозначения

- привязки точек и выводов от угла и от пола, мм
- мебель и приборы — фасад по расстановке (условно)
- окно: проём, рама, подоконник
- стены и перекрытия в сечении
- окраска: тон — цвет по коду производителя (условно)
- О1 — марка отделки по реестру отделки альбома
- А — марка развёртки: буква стены, стрелка — взгляд

Ведомость отделки (на листе)

Марка	Поверхность	Материал, изделие	Цвет, код	Кол.
О1	стены	окраска, Tikkurila Luja 7, шелковисто-матовая, подготовка К3	NCS S 0804-Y30R «S 0804-Y30R»	4,4 м²
О4	потолок	окраска, Tikkurila Luja 7, матовая, подготовка Q3	NCS S 0804-Y30R «S 0804-Y30R»	21,8 м²
О20	плинтус	керамогранит, аналог: плинтус из керамогранита пола, подрезка 80 мм, верхняя кромка с запилом 45°	#B8AFA5 «тон Claystone V486»	2,4 м

Допущения и предложения на листе

Основа листа: размеры и контуры этажей подобраны проектировщиком по составу помещений и площадям этажей с картинки 470 px (размеры на ней не читаются); обмер и исходный проект — задание (К-1); высоты: 1-й этаж 2800 мм, мансарда 2700 мм (горизонтальная часть) приняты; скаты кровли мансарды приняты по картинке: колено 1200 мм, уклон 45°, конёк вдоль длинной стороны; проект КР — задание (К-2); наружные стены 400 мм, перегородки 120 мм приняты (К-1); разрешённая мощность 15 кВт принята по типовым ТУ для частного дома (К-4); подрайон климата не задан — принят не северный (жилые от 2,5 м) (К-7).

См. лист открытых вопросов (лист 7, записи К-1, К-2, К-4, К-7).

Примечания

1. Развёртки — вид на стену изнутри помещения, по часовой стрелке; расположение — на схеме листа и на листе 102; размеры — в мм по чистовым поверхностям; отметки — в м от ±0,000; высоты Н — от чистого пола помещения до оси изделия, у декора — до центра.
2. Красные цепочки — привязки электроточек и выводов: по горизонтали от угла чистовых стен, по вертикали от чистого пола, до оси изделия; звенья короче 3 мм на листе вынесены во второй ярус (ближняя к стене цепочка).
3. У знака электроточки: марка (Р — розетка, S — выключатель, Св — светильник, ЭВ — вывод кабеля), ×N — число постов в рамке, гр. — группа щита, Н — высота оси от чистого пола, мм; группы по клавишам выключателя — на листе выключателей.
4. Схема мебели, приборов и декора не является технической документацией для производства мебели; габариты — по паспортам изделий.

1000 мм · печать 1:1

Изм.	Кол.уч	Лист	№ док.	Подп.	Дата
Разраб.		Кырлан А.С.			21.10.26
Пров.					
ГИП					
Н. контр.					
Утв.					

ГД-2026-010-АИ

Дом 331 м²

Общая площадь 270,67* м² · * размеры приняты, не замерены (реестр — л. 7, К-1)

Дизайн-проект интерьера

Стадия	Лист	Листов
РП	127	159

Развёртка стены Г. Веранда (пом. 11)

М 1:20

Кырлан Александр Сергеевич

выпуск 18.10.2026 № 9365d64cec · стр. 133 из 197

Развёртки стен. Крыльцо (пом. 12)

Крыльцо (пом. 12) · вид изнутри помещения · размеры в мм, отметки в м

ПРЕДВАРИТЕЛЬНО · не для производства работ · открыто пунктов: 6 (реестр — л. 7)

Развёртка стены А

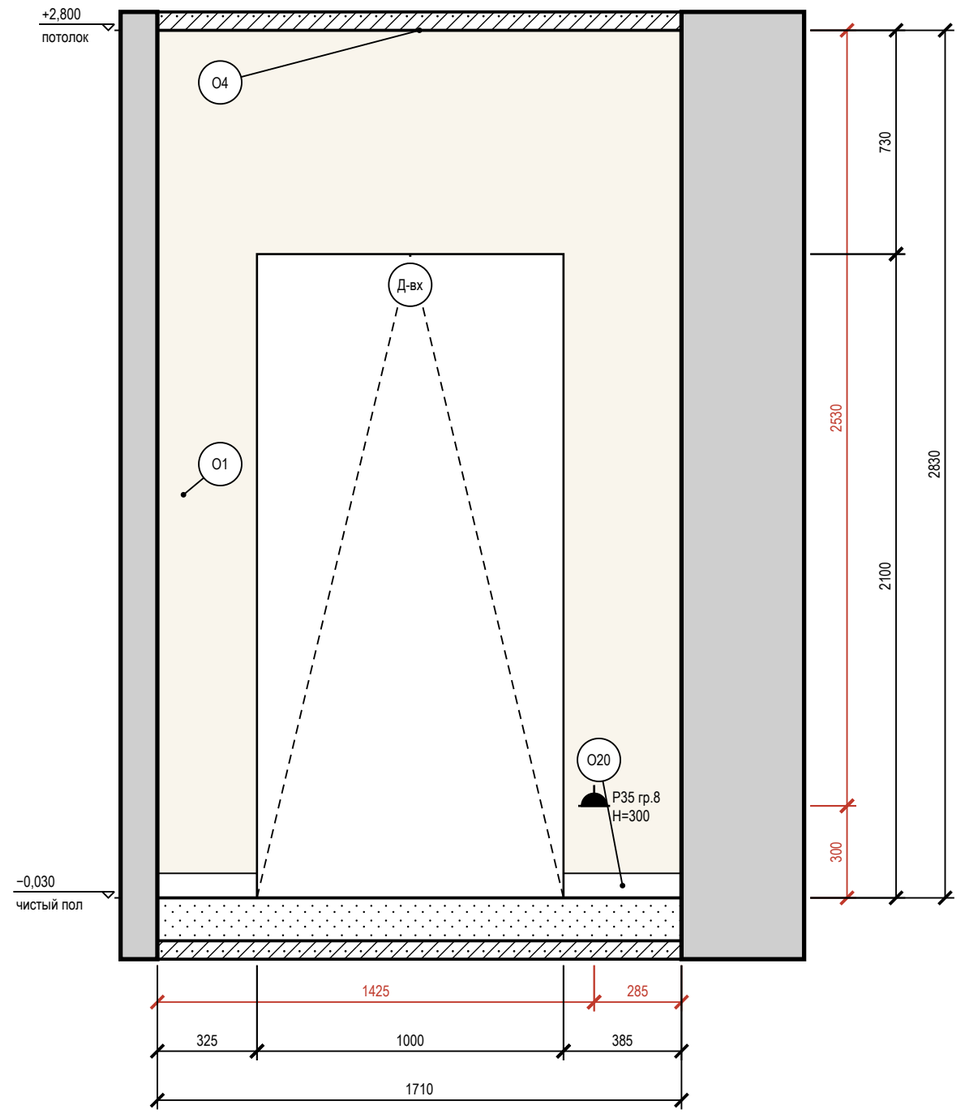

Схема развёрток (М 1:100)

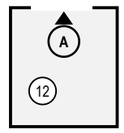

Условные обозначения

- розетка влагозащищённая IP44
- привязки точек и выводов от угла и от пола, мм
- мебель и приборы — фасад по расстановке (условно)
- дверной проём; марка двери — в кружке
- стены и перекрытия в сечении
- окраска: тон — цвет по коду производителя (условно)
- О1 — марка отделки по реестру отделки альбома
- А — марка развёртки: буква стены, стрелка — взгляд

Ведомость отделки (на листе)

Марка	Поверхность	Материал, изделие	Цвет, код	Кол.
О1	стены	окраска, Tikkurila Luja 7, шелковисто-матовая, подготовка К3	NCS S 0804-Y30R «S 0804-Y30R»	2,7 м²
О4	потолок	окраска, Tikkurila Luja 7, матовая, подготовка Q3	NCS S 0804-Y30R «S 0804-Y30R»	3,4 м²
О20	плинтус	керамогранит, аналог: плинтус из керамогранита пола, подрезка 80 мм, верхняя кромка с запилом 45°	#B8AFA5 «тон Claystone V486»	0,7 м

Допущения и предложения на листе

Основа листа: размеры и контуры этажей подобраны проектировщиком по составу помещений и площадям этажей с картинки 470 px (размеры на ней не читаются); обмер и исходный проект — задание (К-1); высоты: 1-й этаж 2800 мм, мансарда 2700 мм (горизонтальная часть) приняты; скаты кровли мансарды приняты по картинке: колено 1200 мм, уклон 45°, конёк вдоль длинной стороны; проект КР — задание (К-2); наружные стены 400 мм, перегородки 120 мм приняты (К-1); разрешённая мощность 15 кВт принята по типовым ТУ для частного дома (К-4); подрайон климата не задан — принят не северный (жилые от 2,5 м) (К-7).

См. лист открытых вопросов (лист 7, записи К-1, К-2, К-4, К-7).

Примечания

1. Развёртки — вид на стену изнутри помещения, по часовой стрелке; расположение — на схеме листа и на листе 102; размеры — в мм по чистовым поверхностям; отметки — в м от ±0,000; высоты Н — от чистого пола помещения до оси изделия, у декора — до центра.
2. Красные цепочки — привязки электроточек и выводов: по горизонтали от угла чистовых стен, по вертикали от чистого пола, до оси изделия; звенья короче 3 мм на листе вынесены во второй ярус (ближняя к стене цепочка).
3. У знака электроточки: марка (Р — розетка, S — выключатель, Св — светильник, ЭВ — вывод кабеля), ×N — число постов в рамке, гр. — группа щита, Н — высота оси от чистого пола, мм; группы по клавишам выключателя — на листе выключателей.
4. Схема мебели, приборов и декора не является технической документацией для производства мебели; габариты — по паспортам изделий.

1000 мм · печать 1:1

Изм.	Кол.уч	Лист	№ док.	Подп.	Дата
Разраб.		Кырлан А.С.			21.10.26
Пров.					
ГИП					
Н. контр.					
Утв.					

ГД-2026-010-АИ

Дом 331 м²

Общая площадь 270,67* м² · * размеры приняты, не замерены (реестр — л. 7, К-1)

Дизайн-проект интерьера	Стадия	Лист	Листов
	РП	128	159

Развёртки стен. Крыльцо (пом. 12)

М 1:20

Кырлан Александр Сергеевич

выпуск 18.10.2026 № 9365d64cec · стр. 134 из 197

Развёртки стен А, Б. Спальня мастер (пом. 13)

Спальня мастер (пом. 13) · вид изнутри помещения · размеры в мм, отметки в м

ПРЕДВАРИТЕЛЬНО · не для производства работ · открыто пунктов: 6 (реестр — л. 7)

Развёртка стены А

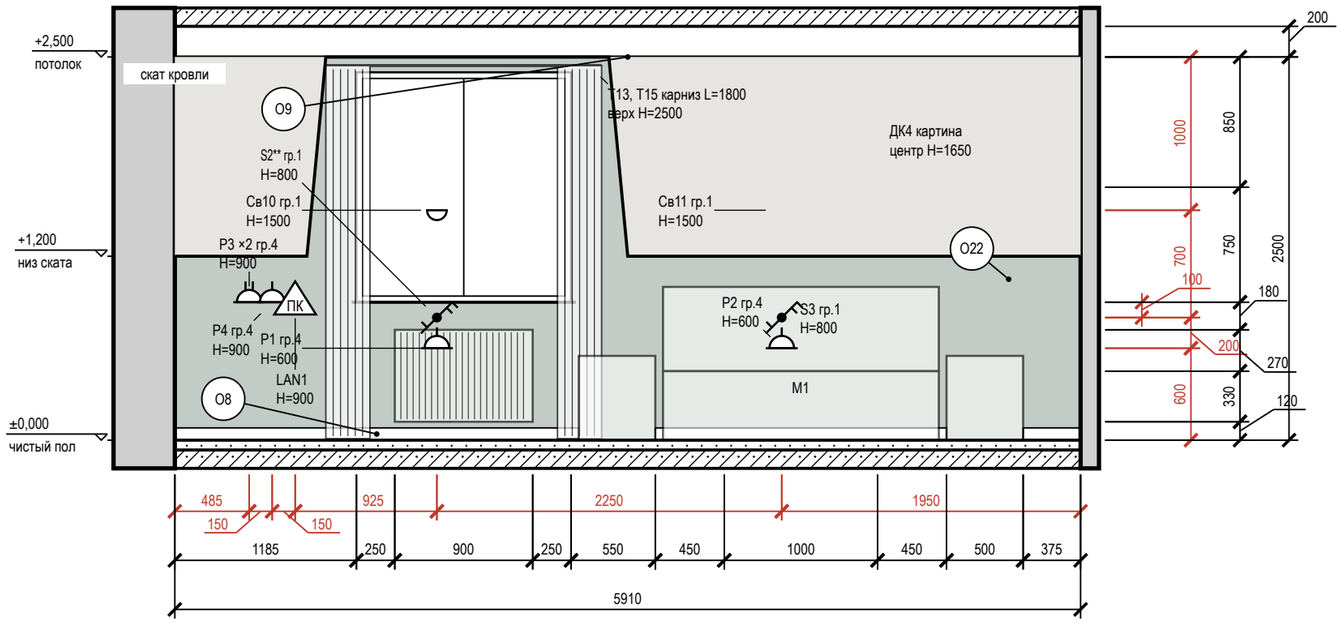

Развёртка стены Б

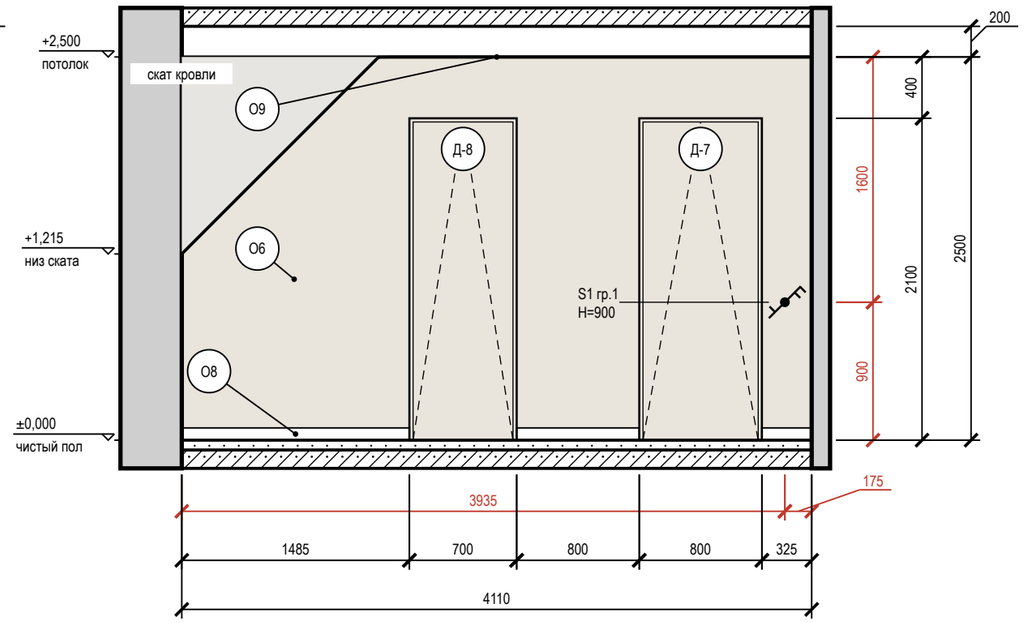

Схема развёрток (М 1:100)

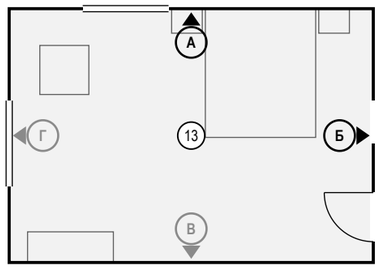

Условные обозначения

- розетка с заземляющим контактом; у знака — марка, ×N постов в рамке, гр. — группа щита, Н — высота оси, мм
- выключатель одноклавишный
- выключатель двухклавишный (флажков — по числу клавиш)
- выключатель с проходной или перекрёстной клавишей (обратный флажок); тип клавиши — в подписи
- светильник настенный (бра), Н — высота оси
- розетка компьютерная RJ45
- привязки точек и выводов от угла и от пола, мм
- мебель и приборы — фасад по расстановке (условно)
- картина (декор): марка Д, крест — центр, Н — высота центра, мм
- карниз (шина) и шторы в собранном виде: марка Т, длина L, верх Н
- дверь скрытого монтажа: полотно в плоскости стены (узел — на листе узлов)
- окно: проём, рама, подоконник
- радиатор отопления; марка — по плану отопления
- стены и перекрытия в сечении
- окраска: тон — цвет по коду производителя (условно)
- О1 — марка отделки по реестру отделки альбома
- А — марка развёртки: буква стены, стрелка — взгляд

Ведомость отделки (на листе)

Марка	Поверхность	Материал, изделие	Цвет, код	Кол.
О6	стены	окраска, Farrow & Ball Modern Emulsion, матовая, подготовка Q3	Farrow & Ball No. 226 «Joa's White»	7,1 м²
О8	плинтус	плинтус МДФ, h 80 мм, аналог: плинтус МДФ под покраску 80×16	Farrow & Ball No. 226 «Joa's White»	7,5 м
О9	потолок	окраска, Tikkurila Anti-Reflex 2, глубокоматовая, подготовка Q3	Little Greene No. 105 «Slaked Lime»	24,6 м²
О22	акцентная стена	окраска, Farrow & Ball Modern Emulsion, матовая, подготовка Q3	NCS S 7020-G10Y «Хвойный тёмно-зелёный»	12,7 м²

Допущения и предложения на листе

Основа листа: размеры и контуры этажей подобраны проектировщиком по составу помещений и площадям этажей с картинки 470 px (размеры на ней не читаются); обмер и исходный проект — задание (К-1); высоты: 1-й этаж 2800 мм, мансарда 2700 мм (горизонтальная часть) приняты; скаты кровли мансарды приняты по картинке: колено 1200 мм, уклон 45°, конёк вдоль длинной стороны; проект КР — задание (К-2); наружные стены 400 мм, перегородки 120 мм приняты (К-1); разрешённая мощность 15 кВт принята по типовым ТУ для частного дома (К-4); подрайон климата не задан — принят не северный (жилые от 2,5 м) (К-7).

Знак «**» — предложение проектировщика, заказчиком не утверждено (согласовать с заказчиком): записи в реестре нет: S2 — светорегулятор добавлен под диммируемую ленту L3; уровни сценариев выбраны конвейером.

См. лист открытых вопросов (лист 7, записи К-1, К-2, К-4, К-7).

Примечания

1. Развёртки — вид на стену изнутри помещения, по часовой стрелке; расположение — на схеме листа и на листе 102; размеры — в мм по чистовым поверхностям; отметки — в м от ±0,000; высоты Н — от чистого пола помещения до оси изделия, у декора — до центра.
2. Красные цепочки — привязки электроточек и выводов: по горизонтали от угла чистовых стен, по вертикали от чистого пола, до оси изделия; звенья короче 3 мм на листе вынесены во второй ярус (ближняя к стене цепочка).
3. У знака электроточки: марка (Р — розетка, S — выключатель, Св — светильник, ЭВ — вывод кабеля), ×N — число постов в рамке, гр. — группа щита, Н — высота оси от чистого пола, мм; группы по клавишам выключателя — на листе выключателей.
4. Схема мебели, приборов и декора не является технической документацией для производства мебели; габариты — по паспортам изделий.
5. Картины и зеркала крепить к основанию по паспорту изделия (закладные и анкеры — в перечне скрытых работ); крест — ось центра предмета.
6. Карнизы (шины) — по ведомости текстиля декоратора; длина L и верх Н — по развёртке, крепление — до окраски потолка.
7. Двери скрытого монтажа — полотно в плоскости стены, отделка стены по полотну, плинтус прерывается у короба (узел — на листе узлов).
8. Потолок на развёртках — по нижнему уровню У1; другие уровни потолка помещения: У2 +2,600.

1000 мм · печать 1:1

Изм.	Кол.уч	Лист	№ док.	Подп.	Дата
Разраб.		Кырлан А.С.			21.10.26
Пров.					
ГИП					
Н. контр.					
Утв.					

ГД-2026-010-АИ

Дом 331 м²

Общая площадь 270,67* м² · * размеры приняты, не замерены (реестр — л. 7, К-1)

Дизайн-проект интерьера

Стадия	Лист	Листов
РП	129	159

Развёртки стен А, Б. Спальня мастер (пом. 13)

М 1:40

Кырлан Александр Сергеевич

выпуск 18.10.2026 № 9365d64cec · стр. 135 из 197

Развёртки стен В, Г. Спальня мастер (пом. 13)

Спальня мастер (пом. 13) · вид изнутри помещения · размеры в мм, отметки в м

ПРЕДВАРИТЕЛЬНО · не для производства работ · открыто пунктов: 6 (реестр — л. 7)

Развёртка стены В

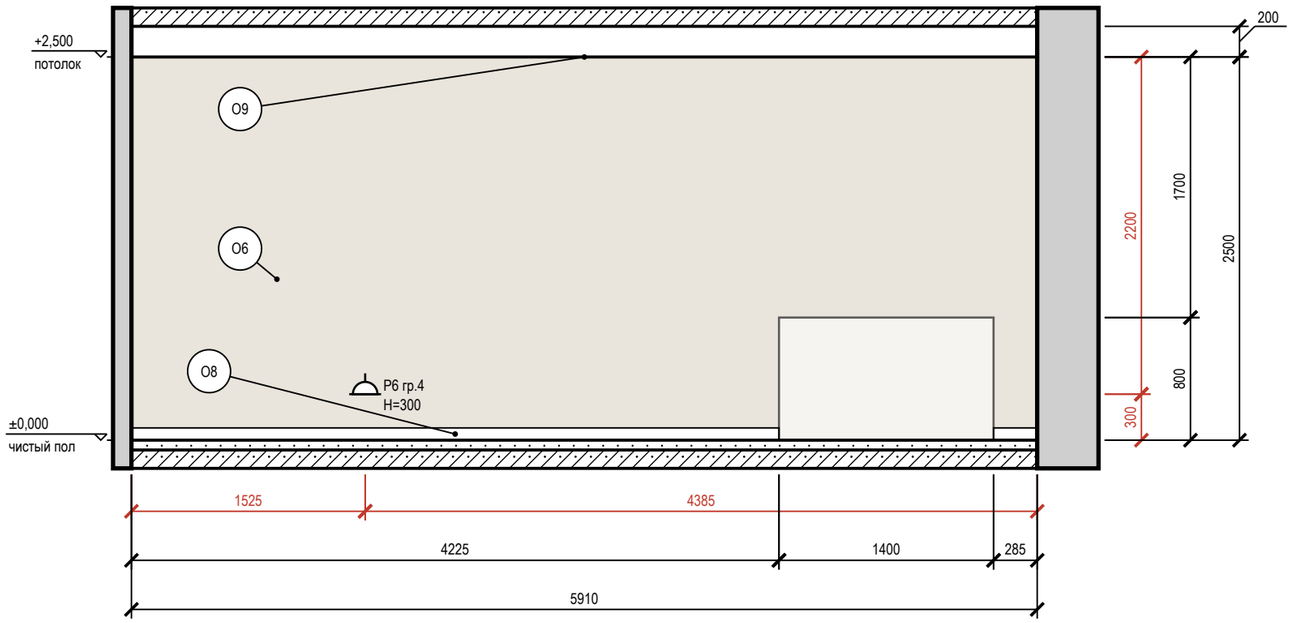

Развёртка стены Г

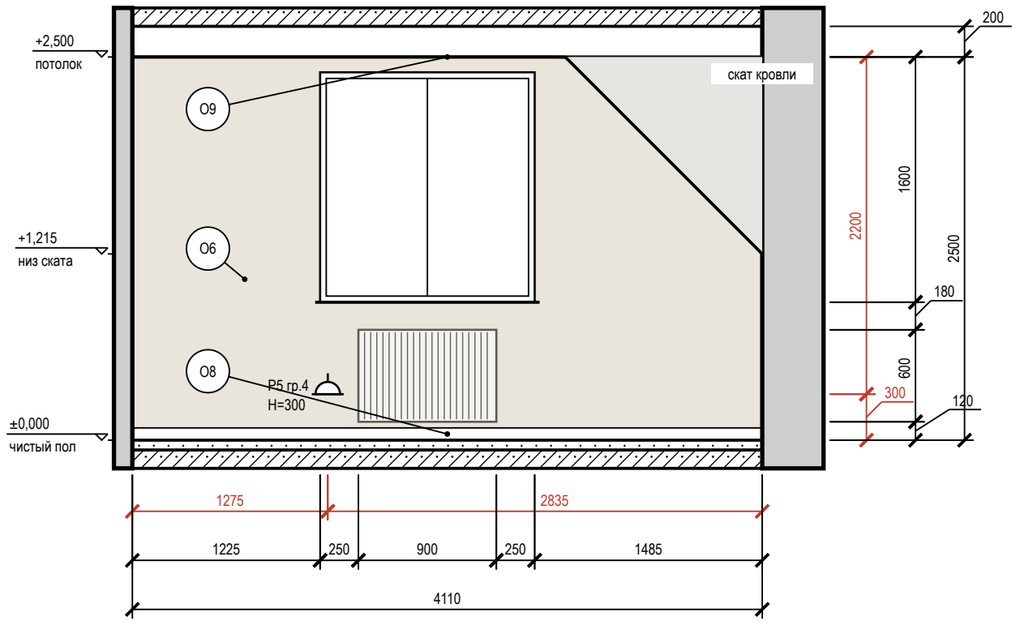

Схема развёрток (М 1:100)

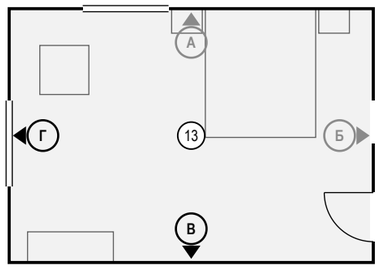

Условные обозначения

- розетка с заземляющим контактом; у знака — марка, ×N постов в рамке, гр. — группа щита, Н — высота оси, мм
- привязки точек и выводов от угла и от пола, мм
- мебель и приборы — фасад по расстановке (условно)
- окно: проём, рама, подоконник
- радиатор отопления; марка — по плану отопления
- стены и перекрытия в сечении
- окраска: тон — цвет по коду производителя (условно)
- О1 — марка отделки по реестру отделки альбома
- А — марка развёртки: буква стены, стрелка — взгляд

Ведомость отделки (на листе)

Марка	Поверхность	Материал, изделие	Цвет, код	Кол.
О6	стены	окраска, Farrow & Ball Modern Emulsion, матовая, подготовка Q3	Farrow & Ball No. 226 «Joa's White»	23 м²
О8	плинтус	плинтус МДФ, h 80 мм, аналог: плинтус МДФ под покраску 80×16	Farrow & Ball No. 226 «Joa's White»	8,6 м
О9	потолок	окраска, Tikkurila Anti-Reflex 2, глубокоматовая, подготовка Q3	Little Greene No. 105 «Slaked Lime»	24,6 м²

Допущения и предложения на листе

Основа листа: размеры и контуры этажей подобраны проектировщиком по составу помещений и площадям этажей с картинки 470 px (размеры на ней не читаются); обмер и исходный проект — задание (К-1); высоты: 1-й этаж 2800 мм, мансарда 2700 мм (горизонтальная часть) приняты; скаты кровли мансарды приняты по картинке: колено 1200 мм, уклон 45°, конёк вдоль длинной стороны; проект КР — задание (К-2); наружные стены 400 мм, перегородки 120 мм приняты (К-1); разрешённая мощность 15 кВт принята по типовым ТУ для частного дома (К-4); подрайон климата не задан — принят не северный (жилые от 2,5 м) (К-7).

См. лист открытых вопросов (лист 7, записи К-1, К-2, К-4, К-7).

Примечания

1. Развёртки — вид на стену изнутри помещения, по часовой стрелке; расположение — на схеме листа и на листе 102; размеры — в мм по чистовым поверхностям; отметки — в м от ±0,000; высоты Н — от чистого пола помещения до оси изделия, у декора — до центра.
2. Красные цепочки — привязки электроточек и выводов: по горизонтали от угла чистовых стен, по вертикали от чистого пола, до оси изделия; звенья короче 3 мм на листе вынесены во второй ярус (ближняя к стене цепочка).
3. У знака электроточки: марка (Р — розетка, S — выключатель, Св — светильник, ЭВ — вывод кабеля), ×N — число постов в рамке, гр. — группа щита, Н — высота оси от чистого пола, мм; группы по клавишам выключателя — на листе выключателей.
4. Схема мебели, приборов и декора не является технической документацией для производства мебели; габариты — по паспортам изделий.
5. Потолок на развёртках — по нижнему уровню У1; другие уровни потолка помещения: У2 +2,600.

1000 мм · печать 1:1

Изм.	Кол.уч	Лист	№ док.	Подп.	Дата
Разраб.		Кырлан А.С.			21.10.26
Пров.					
ГИП					
Н. контр.					
Утв.					

ГД-2026-010-АИ

Дом 331 м²

Общая площадь 270,67* м² · * размеры приняты, не замерены (реестр — л. 7, К-1)

Дизайн-проект интерьера

Стадия	Лист	Листов
РП	130	159

Развёртки стен В, Г. Спальня мастер (пом. 13)

М 1:40

Кырлан Александр Сергеевич

выпуск 18.10.2026 № 9365d64cec · стр. 136 из 197

Развёртки стен А, Б, В. Гардеробная мастер (пом. 14)

Гардеробная мастер (пом. 14) · вид изнутри помещения · размеры в мм, отметки в м

ПРЕДВАРИТЕЛЬНО · не для производства работ · открыто пунктов: 6 (реестр — л. 7)

Развёртка стены А

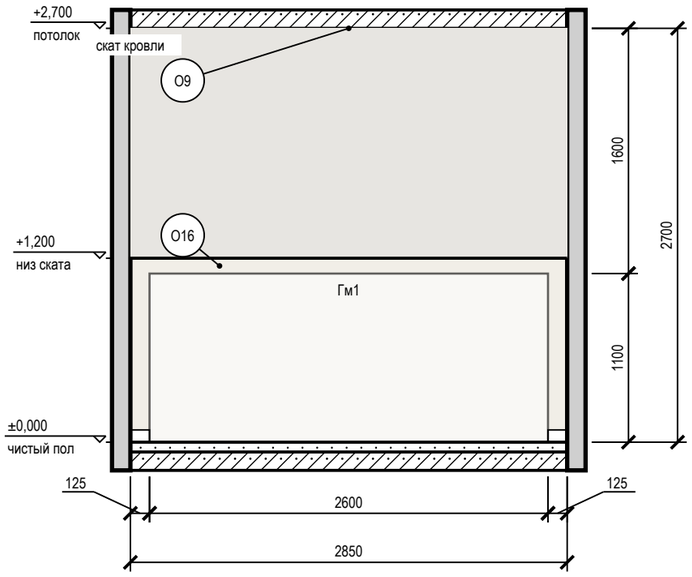

Развёртка стены Б

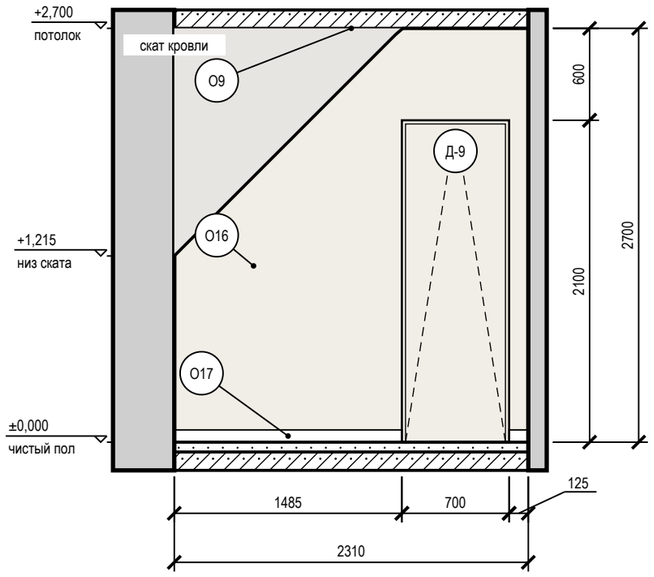

Развёртка стены В

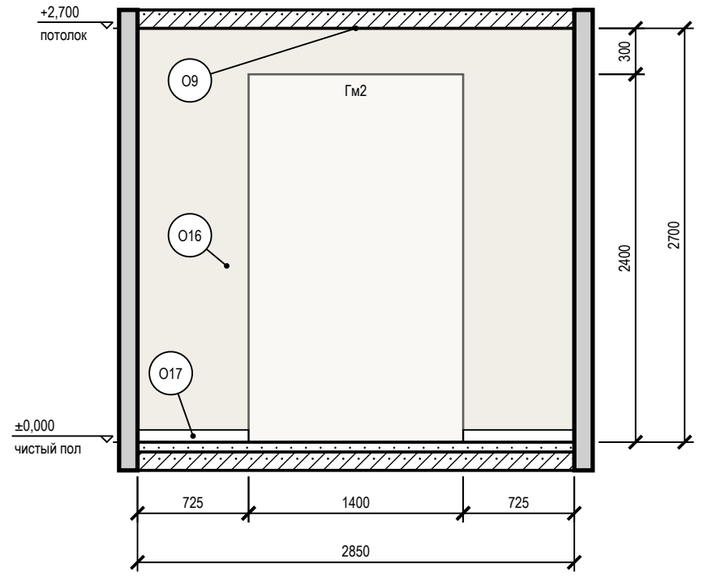

Схема развёрток (М 1:100)

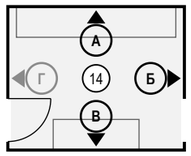

Условные обозначения

- привязки точек и выводов от угла и от пола, мм
- мебель и приборы — фасад по расстановке (условно)
- дверь скрытого монтажа: полотно в плоскости стены (узел — на листе узлов)
- стены и перекрытия в сечении
- окраска: тон — цвет по коду производителя (условно)
- О1 — марка отделки по реестру отделки альбома
- А — марка развёртки: буква стены, стрелка — взгляд

Ведомость отделки (на листе)

Марка	Поверхность	Материал, изделие	Цвет, код	Кол.
О9	потолок	окраска, Tikkurila Anti-Reflex 2, глубокоматовая, подготовка Q3	Little Greene No. 105 «Slaked Lime»	6,7 м²
О16	стены	окраска, Tikkurila Harmony, матовая, подготовка Q3	Little Greene No. 105 «Slaked Lime»	20,2 м²
О17	плинтус	плинтус МДФ, h 80 мм, аналог: плинтус МДФ под покраску 80×16	Little Greene No. 105 «Slaked Lime»	3,3 м

Допущения и предложения на листе

Основа листа: размеры и контуры этажей подобраны проектировщиком по составу помещений и площадям этажей с картинки 470 px (размеры на ней не читаются); обмер и исходный проект — задание (К-1); высоты: 1-й этаж 2800 мм, мансарда 2700 мм (горизонтальная часть) приняты; скаты кровли мансарды приняты по картинке: колено 1200 мм, уклон 45°, конёк вдоль длинной стороны; проект КР — задание (К-2); наружные стены 400 мм, перегородки 120 мм приняты (К-1); разрешённая мощность 15 кВт принята по типовым ТУ для частного дома (К-4); подрайон климата не задан — принят не северный (жилые от 2,5 м) (К-7).

См. лист открытых вопросов (лист 7, записи К-1, К-2, К-4, К-7).

Примечания

1. Развёртки — вид на стену изнутри помещения, по часовой стрелке; расположение — на схеме листа и на листе 102; размеры — в мм по чистовым поверхностям; отметки — в м от ±0,000; высоты Н — от чистого пола помещения до оси изделия, у декора — до центра.
2. Красные цепочки — привязки электроточек и выводов: по горизонтали от угла чистовых стен, по вертикали от чистого пола, до оси изделия; звенья короче 3 мм на листе вынесены во второй ярус (ближняя к стене цепочка).
3. У знака электроточки: марка (Р — розетка, S — выключатель, Св — светильник, ЭВ — вывод кабеля), ×N — число постов в рамке, гр. — группа щита, Н — высота оси от чистого пола, мм; группы по клавишам выключателя — на листе выключателей.
4. Схема мебели, приборов и декора не является технической документацией для производства мебели; габариты — по паспортам изделий.
5. Двери скрытого монтажа — полотно в плоскости стены, отделка стены по полотну, плинтус прерывается у короба (узел — на листе узлов).

1000 мм · печать 1:1

Изм.	Кол.уч	Лист	№ док.	Подп.	Дата
Разраб.		Кырлан А.С.			21.10.26
Пров.					
ГИП					
Н. контр.					
Утв.					

ГД-2026-010-АИ

Дом 331 м²

Общая площадь 270,67* м² · * размеры приняты, не замерены (реестр — л. 7, К-1)

Дизайн-проект интерьера

Стадия	Лист	Листов
РП	131	159

Развёртки стен А, Б, В. Гардеробная мастер (пом. 14)

М 1:40

Кырлан Александр Сергеевич

выпуск 18.10.2026 № 9365d64cec · стр. 137 из 197

Развёртка стены Г. Гардеробная мастер (пом. 14)

Гардеробная мастер (пом. 14) · вид изнутри помещения · размеры в мм, отметки в м

ПРЕДВАРИТЕЛЬНО · не для производства работ · открыто пунктов: 6 (реестр — л. 7)

Развёртка стены Г

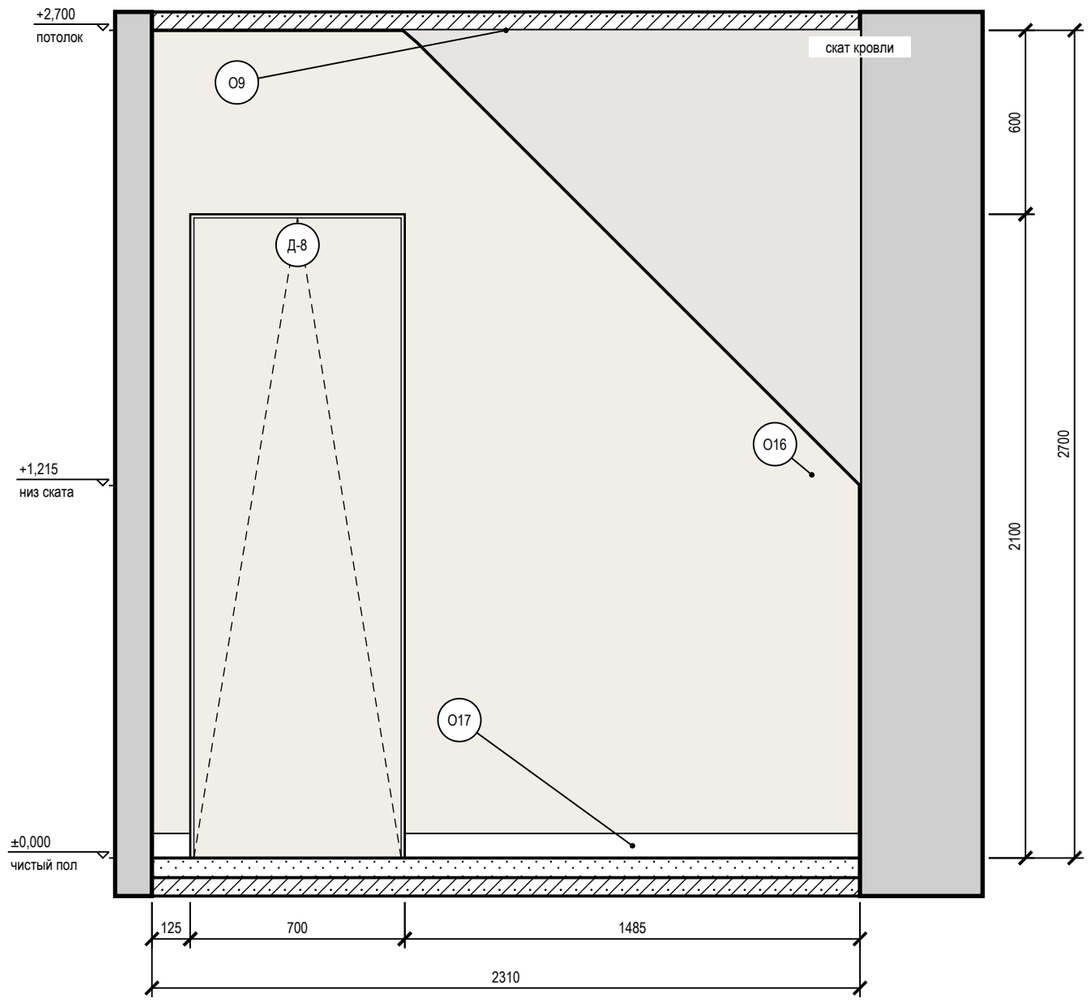

Схема развёрток (М 1:100)

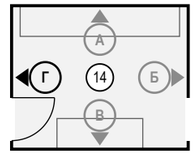

Условные обозначения

- привязки точек и выводов от угла и от пола, мм
- мебель и приборы — фасад по расстановке (условно)
- дверь скрытого монтажа: полотно в плоскости стены (узел — на листе узлов)
- стены и перекрытия в сечении
- окраска: тон — цвет по коду производителя (условно)
- О1 — марка отделки по реестру отделки альбома
- А — марка развёртки: буква стены, стрелка — взгляд

Ведомость отделки (на листе)

Марка	Поверхность	Материал, изделие	Цвет, код	Кол.
О9	потолок	окраска, Tikkurila Anti-Reflex 2, глубокоматовая, подготовка Q3	Little Greene No. 105 «Slaked Lime»	6,7 м²
О16	стены	окраска, Tikkurila Harmony, матовая, подготовка Q3	Little Greene No. 105 «Slaked Lime»	4,8 м²
О17	плинтус	плинтус МДФ, h 80 мм, аналог: плинтус МДФ под покраску 80×16	Little Greene No. 105 «Slaked Lime»	1,6 м

Допущения и предложения на листе

Основа листа: размеры и контуры этажей подобраны проектировщиком по составу помещений и площадям этажей с картинки 470 px (размеры на ней не читаются); обмер и исходный проект — задание (К-1); высоты: 1-й этаж 2800 мм, мансарда 2700 мм (горизонтальная часть) приняты; скаты кровли мансарды приняты по картинке: колено 1200 мм, уклон 45°, конёк вдоль длинной стороны; проект КР — задание (К-2); наружные стены 400 мм, перегородки 120 мм приняты (К-1); разрешённая мощность 15 кВт принята по типовым ТУ для частного дома (К-4); подрайон климата не задан — принят не северный (жилые от 2,5 м) (К-7).

См. лист открытых вопросов (лист 7, записи К-1, К-2, К-4, К-7).

Примечания

1. Развёртки — вид на стену изнутри помещения, по часовой стрелке; расположение — на схеме листа и на листе 102; размеры — в мм по чистовым поверхностям; отметки — в м от ±0,000; высоты Н — от чистого пола помещения до оси изделия, у декора — до центра.
2. Красные цепочки — привязки электроточек и выводов: по горизонтали от угла чистовых стен, по вертикали от чистого пола, до оси изделия; звенья короче 3 мм на листе вынесены во второй ярус (ближняя к стене цепочка).
3. У знака электроточки: марка (Р — розетка, S — выключатель, Св — светильник, ЭВ — вывод кабеля), ×N — число постов в рамке, гр. — группа щита, Н — высота оси от чистого пола, мм; группы по клавишам выключателя — на листе выключателей.
4. Схема мебели, приборов и декора не является технической документацией для производства мебели; габариты — по паспортам изделий.
5. Двери скрытого монтажа — полотно в плоскости стены, отделка стены по полотну, плинтус прерывается у короба (узел — на листе узлов).

1000 мм · печать 1:1

Изм.	Кол.уч	Лист	№ док.	Подп.	Дата
Разраб.		Кырлан А.С.			21.10.26
Пров.					
ГИП					
Н. контр.					
Утв.					

ГД-2026-010-АИ

Дом 331 м²

Общая площадь 270,67* м² · * размеры приняты, не замерены (реестр — л. 7, К-1)

Дизайн-проект интерьера

Стадия	Лист	Листов
РП	132	159

Развёртка стены Г. Гардеробная мастер (пом. 14)

М 1:20

Кырлан Александр Сергеевич

выпуск 18.10.2026 № 9365d64cec · стр. 138 из 197

Развёртка стены А. Санузел мастер (пом. 15)

Санузел мастер (пом. 15) · вид изнутри помещения · размеры в мм, отметки в м

ПРЕДВАРИТЕЛЬНО · не для производства работ · открыто пунктов: 6 (реестр — л. 7)

Развёртка стены А

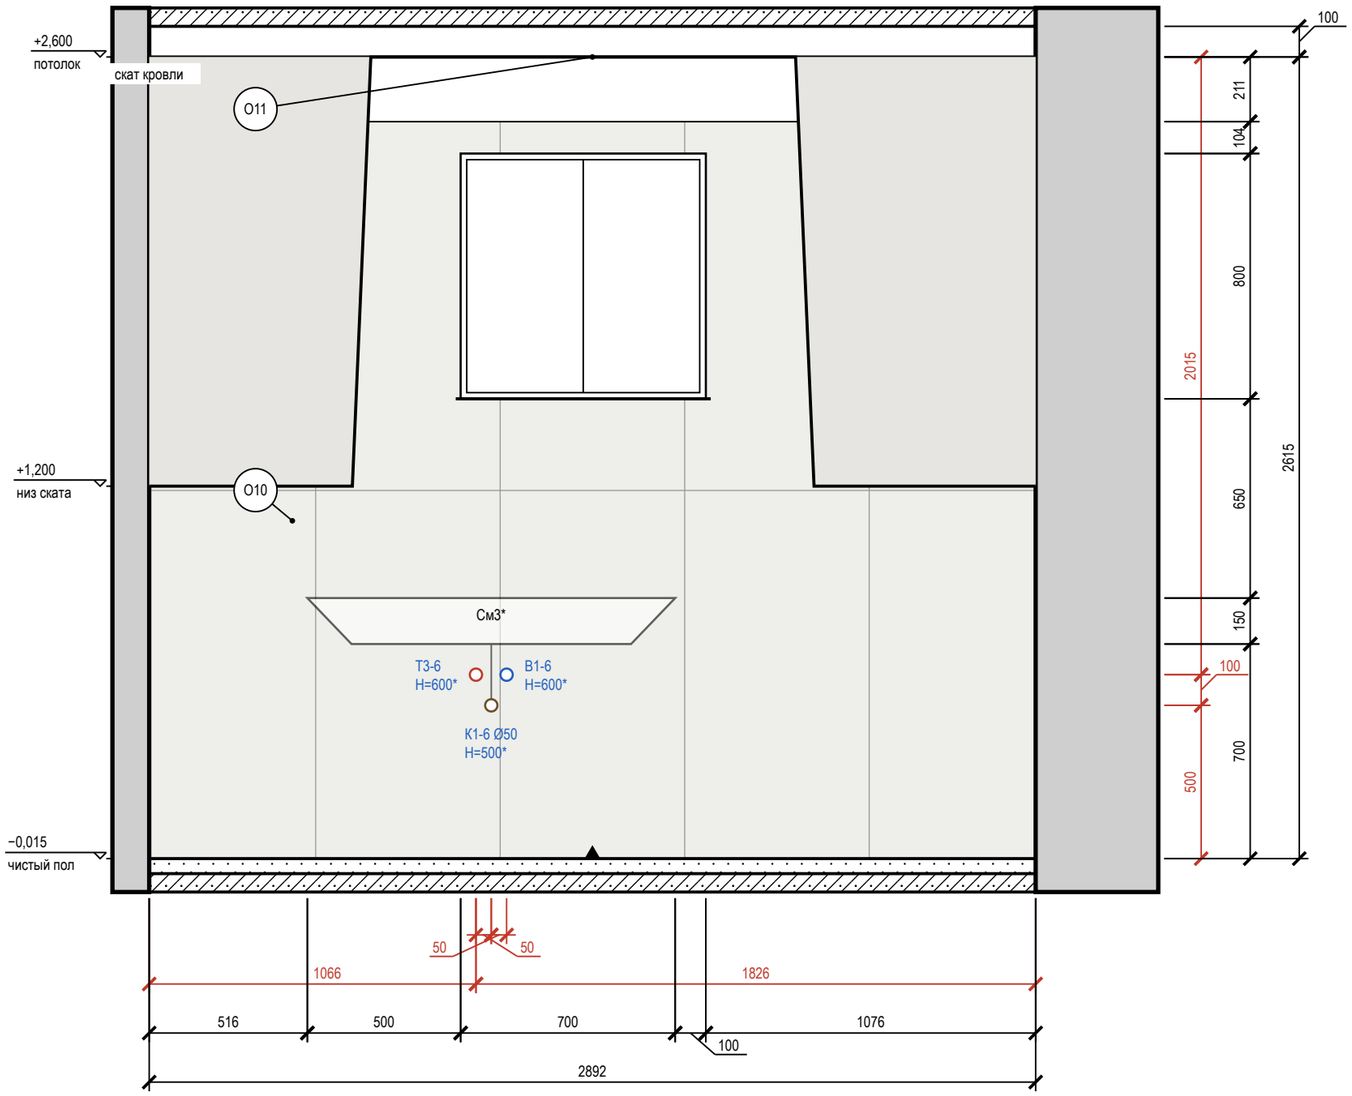

Схема развёрток (М 1:100)

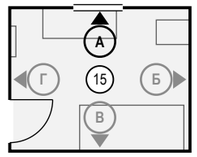

Условные обозначения

- вывод В1 (код — в ведомости привязок)
- вывод Т3 (код — в ведомости привязок)
- вывод К1 (код — в ведомости привязок)
- привязки точек и выводов от угла и от пола, мм
- мебель и приборы — фасад по расстановке (условно)
- окно: проём, рама, подоконник
- стены и перекрытия в сечении
- плитка: сетка швов по формату, ▲ — ось старта
- О1 — марка отделки по реестру отделки альбома
- А — марка развёртки: буква стены, стрелка — взгляд

Ведомость отделки (на листе)

Марка	Поверхность	Материал, изделие	Цвет, код	Кол.
О10	стены	облицовка плиткой, Atlas Concorde Marvel Travertine, 600×1200×9 мм, A8UZ, затирка CG2WA	Atlas Concorde A8UZ «Marvel Travertine»	6,3 м²
О11	потолок	окраска, Tikkurila Luja 7, матовая, подготовка Q3	Little Greene No. 105 «Slaked Lime»	6,9 м²

Допущения и предложения на листе

Основа листа: размеры и контуры этажей подобраны проектировщиком по составу помещений и площадям этажей с картинки 470 px (размеры на ней не читаются); обмер и исходный проект — задание (К-1); высоты: 1-й этаж 2800 мм, мансарда 2700 мм (горизонтальная часть) приняты; скаты кровли мансарды приняты по картинке: колено 1200 мм, уклон 45°, конёк вдоль длинной стороны; проект КР — задание (К-2); наружные стены 400 мм, перегородки 120 мм приняты (К-1); разрешённая мощность 15 кВт принята по типовым ТУ для частного дома (К-4); подрайон климата не задан — принят не северный (жилые от 2,5 м) (К-7).

См. лист открытых вопросов (лист 7, записи К-1, К-2, К-4, К-7).

Примечания

1. Развёртки — вид на стену изнутри помещения, по часовой стрелке; расположение — на схеме листа и на листе 102; размеры — в мм по чистовым поверхностям; отметки — в м от ±0,000; высоты Н — от чистого пола помещения до оси изделия, у декора — до центра.
2. Красные цепочки — привязки электроточек и выводов: по горизонтали от угла чистовых стен, по вертикали от чистого пола, до оси изделия; звенья короче 3 мм на листе вынесены во второй ярус (ближняя к стене цепочка).
3. У знака электроточки: марка (Р — розетка, S — выключатель, Св — светильник, ЭВ — вывод кабеля), ×N — число постов в рамке, гр. — группа щита, Н — высота оси от чистого пола, мм; группы по клавишам выключателя — на листе выключателей.
4. Схема мебели, приборов и декора не является технической документацией для производства мебели; габариты — по паспортам изделий (* — высота не задана в проекте, показана по типовому изделию).
5. Выводы ВК — коды и высоты по листу выводов сантехники; * — высота принята по типовой практике монтажа, окончательно — по паспорту прибора.
6. Облицовка — по сетке швов 2 мм, раскладка от оси стены (треугольник у пола), целые ряды от пола; подрезки — по листу раскладки плитки.
7. Гидроизоляция в 2 слоя, заход на стены 200 мм — до облицовки, с актом скрытых работ и тестом проливом (узел — на листе узлов).

1000 мм · печать 1:1

Изм.	Кол.уч	Лист	№ док.	Подп.	Дата
Разраб.		Кырлан А.С.			21.10.26
Пров.					
ГИП					
Н. контр.					
Утв.					

ГД-2026-010-АИ

Дом 331 м²

Общая площадь 270,67* м² · * размеры приняты, не замерены (реестр — л. 7, К-1)

Дизайн-проект интерьера

Стадия	Лист	Листов
РП	133	159

Развёртка стены А. Санузел мастер (пом. 15)

М 1:20

Кырлан Александр Сергеевич

выпуск 18.10.2026 № 9365d64cec · стр. 139 из 197

Развёртка стены Б. Санузел мастер (пом. 15)

Санузел мастер (пом. 15) · вид изнутри помещения · размеры в мм, отметки в м

ПРЕДВАРИТЕЛЬНО · не для производства работ · открыто пунктов: 6 (реестр — л. 7)

Развёртка стены Б

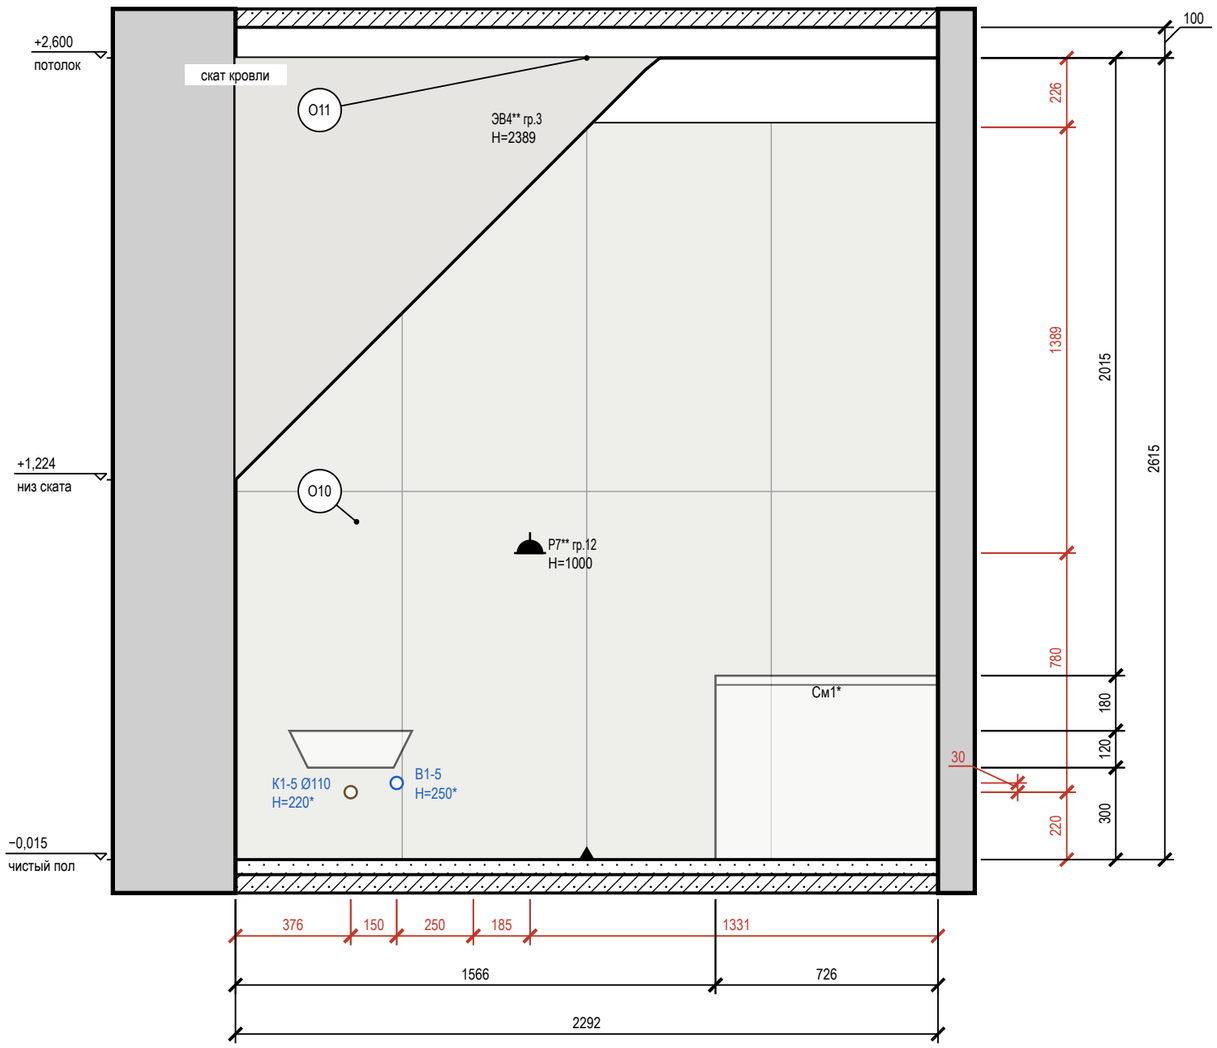

Схема развёрток (М 1:100)

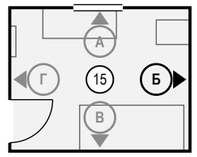

Условные обозначения

- розетка влагозащищённая IP44
- вывод кабеля для подключения прибора (без розетки), марка ЭВ
- вывод В1 (код — в ведомости привязок)
- вывод К1 (код — в ведомости привязок)
- привязки точек и выводов от угла и от пола, мм
- мебель и приборы — фасад по расстановке (условно)
- стены и перекрытия в сечении
- плитка: сетка швов по формату, ▲ — ось старта
- О1 — марка отделки по реестру отделки альбома
- А — марка развёртки: буква стены, стрелка — взгляд

Ведомость отделки (на листе)

Марка	Поверхность	Материал, изделие	Цвет, код	Кол.
О10	стены	облицовка плиткой, Atlas Concorde Marvel Travertine, 600×1200×9 мм, A8UZ, затирка CG2WA	Atlas Concorde A8UZ «Marvel Travertine»	5,5 м²
О11	потолок	окраска, Tikkurila Luja 7, матовая, подготовка Q3	Little Greene No. 105 «Slaked Lime»	6,9 м²

Допущения и предложения на листе

Основа листа: размеры и контуры этажей подобраны проектировщиком по составу помещений и площадям этажей с картинки 470 px (размеры на ней не читаются); обмер и исходный проект — задание (К-1); высоты: 1-й этаж 2800 мм, мансарда 2700 мм (горизонтальная часть) приняты; скаты кровли мансарды приняты по картинке: колено 1200 мм, уклон 45°, конёк вдоль длинной стороны; проект КР — задание (К-2); наружные стены 400 мм, перегородки 120 мм приняты (К-1); разрешённая мощность 15 кВт принята по типовым ТУ для частного дома (К-4); подрайон климата не задан — принят не северный (жилые от 2,5 м) (К-7).

Знак «**» — предложение проектировщика, заказчиком не утверждено (согласовать с заказчиком): записи в реестре нет: Р7 — по образцу: Р7, Р8 и Р33 на высоте 1000 мм — верхний предел нормы (ПУЭ, п. 6.6.30, не выше 1 м); флаг решения снят; ЭВ4 — по образцу: Добавлены выводы к вентиляторам: ЭВ4 (ВР1, ванная) и ЭВ5 (ВР3, санузел 2) — группа 3, высота 2389 мм, включение с основным светом, таймер выбега в вентиляторе; и коробки уравнивания потенциалов КУП1 (ванная) и КУП2 (санузел 2) — высота 300 мм, у входа, вне зон 0–2, проводник от шины РЕ щита ЩК, сече. См. лист открытых вопросов (лист 7, записи К-1, К-2, К-4, К-7).

Примечания

1. Развёртки — вид на стену изнутри помещения, по часовой стрелке; расположение — на схеме листа и на листе 102; размеры — в мм по чистовым поверхностям; отметки — в м от ±0,000; высоты Н — от чистого пола помещения до оси изделия, у декора — до центра.
2. Красные цепочки — привязки электроточек и выводов: по горизонтали от угла чистовых стен, по вертикали от чистого пола, до оси изделия; звенья короче 3 мм на листе вынесены во второй ярус (ближняя к стене цепочка).
3. У знака электроточки: марка (Р — розетка, S — выключатель, Св — светильник, ЭВ — вывод кабеля), ×N — число постов в рамке, гр. — группа щита, Н — высота оси от чистого пола, мм; группы по клавишам выключателя — на листе выключателей.
4. Схема мебели, приборов и декора не является технической документацией для производства мебели; габариты — по паспортам изделий (* — высота не задана в проекте, показана по типовому изделию).
5. Выводы ВК — коды и высоты по листу выводов сантехники; * — высота принята по типовой практике монтажа, окончательно — по паспорту прибора.
6. Облицовка — по сетке швов 2 мм, раскладка от оси стены (треугольник у пола), целые ряды от пола; подрезки — по листу раскладки плитки.
7. Гидроизоляция в 2 слоя, заход на стены 200 мм — до облицовки, с актом скрытых работ и тестом проливом (узел — на листе узлов).

1000 мм · печать 1:1

Изм.	Кол.уч	Лист	№ док.	Подп.	Дата
Разраб.		Кырлан А.С.			21.10.26
Пров.					
ГИП					
Н. контр.					
Утв.					

ГД-2026-010-АИ

Дом 331 м²

Общая площадь 270,67* м² · * размеры приняты, не замерены (реестр — л. 7, К-1)

Дизайн-проект интерьера

Стадия	Лист	Листов
РП	134	159

Развёртка стены Б. Санузел мастер (пом. 15)

М 1:20

Кырлан Александр Сергеевич

выпуск 18.10.2026 № 9365d64cec · стр. 140 из 197

Развёртка стены В. Санузел мастер (пом. 15)

Санузел мастер (пом. 15) · вид изнутри помещения · размеры в мм, отметки в м

ПРЕДВАРИТЕЛЬНО · не для производства работ · открыто пунктов: 6 (реестр — л. 7)

Развёртка стены В

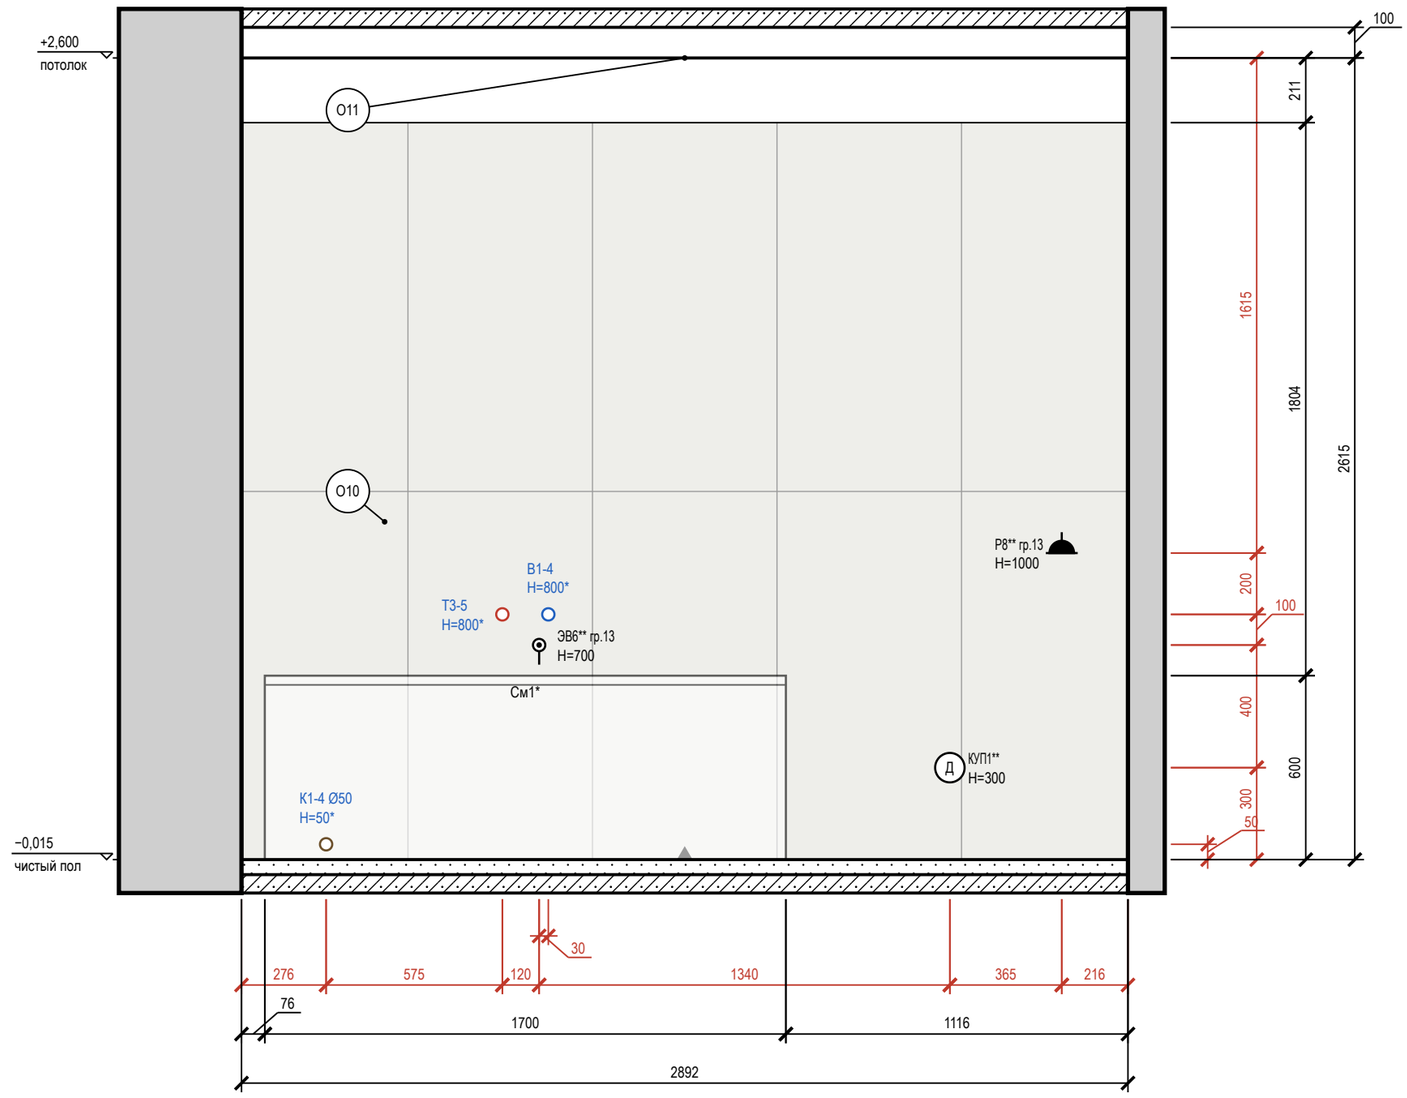

Схема развёрток (М 1:100)

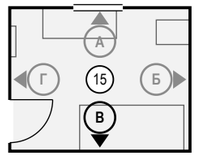

Условные обозначения

- розетка влагозащищённая IP44
- вывод кабеля для подключения прибора (без розетки), марка ЭВ
- вывод В1 (код — в ведомости привязок)
- вывод Т3 (код — в ведомости привязок)
- вывод К1 (код — в ведомости привязок)
- привязки точек и выводов от угла и от пола, мм
- мебель и приборы — фасад по расстановке (условно)
- стены и перекрытия в сечении
- плитка: сетка швов по формату, ▲ — ось старта
- О1 — марка отделки по реестру отделки альбома
- А — марка развёртки: буква стены, стрелка — взгляд

Ведомость отделки (на листе)

Марка	Поверхность	Материал, изделие	Цвет, код	Кол.
О10	стены	облицовка плиткой, Atlas Concorde Marvel Travertine, 600×1200×9 мм, A8UZ, затирка CG2WA	Atlas Concorde A8UZ «Marvel Travertine»	7 м²
О11	потолок	окраска, Tikkurila Luja 7, матовая, подготовка Q3	Little Greene No. 105 «Slaked Lime»	6,9 м²

Допущения и предложения на листе. Основа листа: размеры и контуры этажей подобраны проектировщиком по составу помещений и площадям этажей с картинки 470 px (размеры на ней не читаются); обмер и исходный проект — задание (К-1); высоты: 1-й этаж 2800 мм, мансарда 2700 мм (горизонтальная часть) приняты; скаты кровли мансарды приняты по картинке: колено 1200 мм, уклон 45°, конёк вдоль длинной стороны; проект КР — задание (К-2); наружные стены 400 мм, перегородки 120 мм приняты (К-1); разрешённая мощность 15 кВт принята по типовым ТУ для частного дома (К-4); подрайон климата не задан — принят не северный (жилые от 2,5 м) (К-7). Знак «**» — предложено, не утверждено (согласовать): записи в реестре нет: Р8, КУП1, ЭВ6. См. лист открытых вопросов (лист 7, записи К-1, К-2, К-4, К-7).

Примечания

1. Развёртки — вид на стену изнутри помещения, по часовой стрелке; расположение — на схеме листа и на листе 102; размеры — в мм по чистовым поверхностям; отметки — в м от ±0,000; высоты Н — от чистого пола помещения до оси изделия, у декора — до центра.
2. Красные цепочки — привязки электроточек и выводов: по горизонтали от угла чистовых стен, по вертикали от чистого пола, до оси изделия; звенья короче 3 мм на листе вынесены во второй ярус (ближняя к стене цепочка).
3. У знака электроточки: марка (Р — розетка, S — выключатель, Св — светильник, ЭВ — вывод кабеля), ×N — число постов в рамке, гр. — группа щита, Н — высота оси от чистого пола, мм; группы по клавишам выключателя — на листе выключателей.
4. Схема мебели, приборов и декора не является технической документацией для производства мебели; габариты — по паспортам изделий (* — высота не задана в проекте, показана по типовому изделию).
5. Выводы ВК — коды и высоты по листу выводов сантехники; * — высота принята по типовой практике монтажа, окончательно — по паспорту прибора.
6. Облицовка — по сетке швов 2 мм, раскладка от оси стены (треугольник у пола), целые ряды от пола; подрезки — по листу раскладки плитки.
7. Гидроизоляция в 2 слоя, заход на стены 200 мм — до облицовки, с актом скрытых работ и тестом проливом (узел — на листе узлов).

1000 мм · печать 1:1

Изм.	Кол.уч	Лист	№ док.	Подп.	Дата
Разраб.		Кырлан А.С.			21.10.26
Пров.					
ГИП					
Н. контр.					
Утв.					

ГД-2026-010-АИ

Дом 331 м²

Общая площадь 270,67* м² · * размеры приняты, не замерены (реестр — л. 7, К-1)

Дизайн-проект интерьера

Стадия	Лист	Листов
РП	135	159

Развёртка стены В. Санузел мастер (пом. 15)

М 1:20

Кырлан Александр Сергеевич

выпуск 18.10.2026 № 9365d64cec · стр. 141 из 197

Развёртка стены Г. Санузел мастер (пом. 15)

Санузел мастер (пом. 15) · вид изнутри помещения · размеры в мм, отметки в м

ПРЕДВАРИТЕЛЬНО · не для производства работ · открыто пунктов: 6 (реестр — л. 7)

Развёртка стены Г

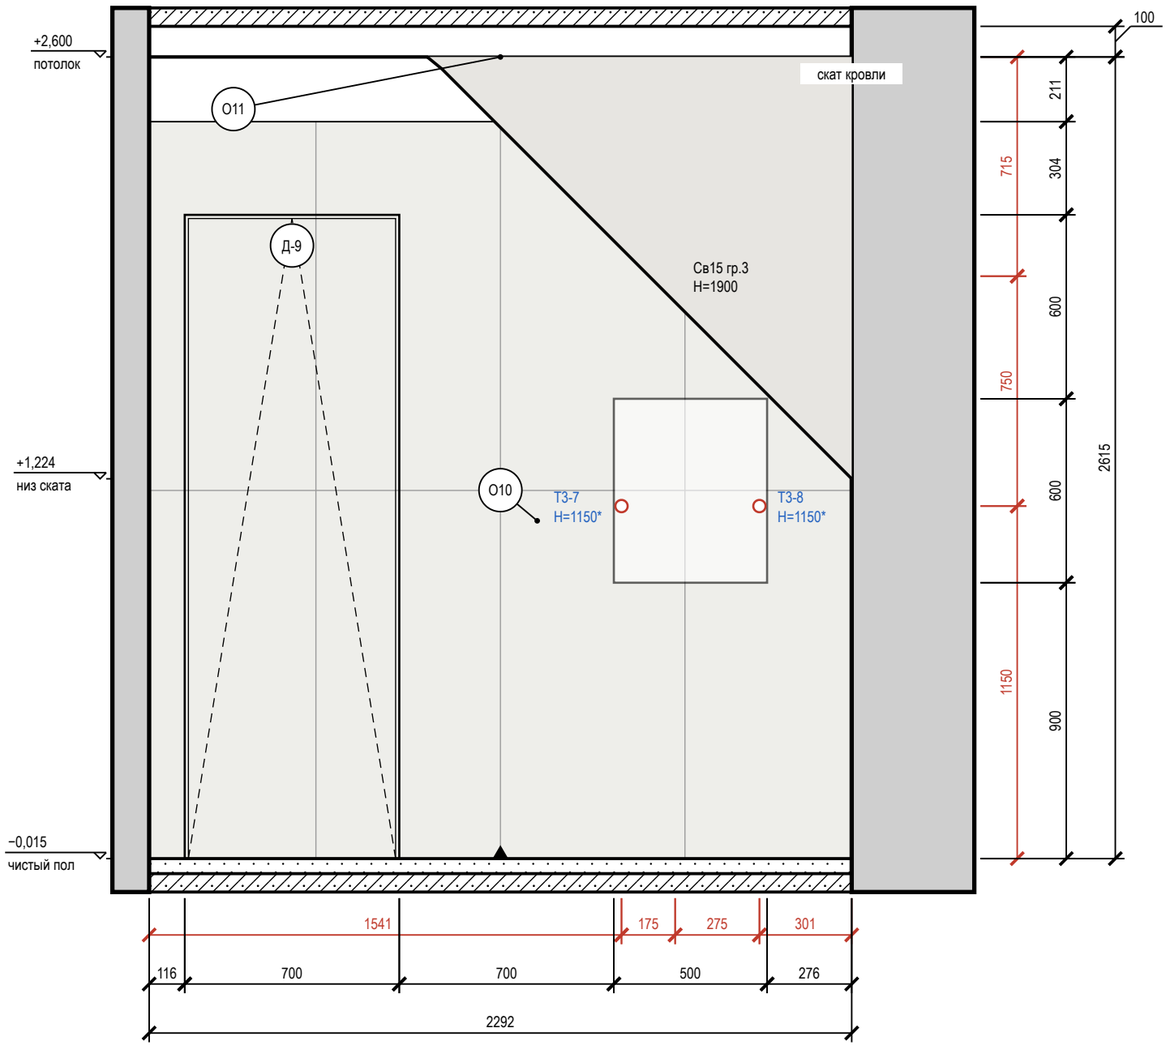

Схема развёрток (М 1:100)

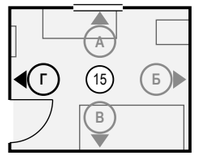

Условные обозначения

- светильник настенный (бра), Н — высота оси
- вывод Т3 (код — в ведомости привязок)
- привязки точек и выводов от угла и от пола, мм
- мебель и приборы — фасад по расстановке (условно)
- дверь скрытого монтажа: полотно в плоскости стены (узел — на листе узлов)
- стены и перекрытия в сечении
- плитка: сетка швов по формату, ▲ — ось старта
- О1 — марка отделки по реестру отделки альбома
- А — марка развёртки: буква стены, стрелка — взгляд

Ведомость отделки (на листе)

Марка	Поверхность	Материал, изделие	Цвет, код	Кол.
О10	стены	облицовка плиткой, Atlas Concorde Marvel Travertine, 600×1200×9 мм, А8UZ, затирка CG2WA	Atlas Concorde A8UZ «Marvel Travertine»	4 м²
О11	потолок	окраска, Tikkurila Luja 7, матовая, подготовка Q3	Little Greene No. 105 «Slaked Lime»	6,9 м²

Допущения и предложения на листе

Основа листа: размеры и контуры этажей подобраны проектировщиком по составу помещений и площадям этажей с картинки 470 px (размеры на ней не читаются); обмер и исходный проект — задание (К-1); высоты: 1-й этаж 2800 мм, мансарда 2700 мм (горизонтальная часть) приняты; скаты кровли мансарды приняты по картинке: колено 1200 мм, уклон 45°, конёк вдоль длинной стороны; проект КР — задание (К-2); наружные стены 400 мм, перегородки 120 мм приняты (К-1); разрешённая мощность 15 кВт принята по типовым ТУ для частного дома (К-4); подрайон климата не задан — принят не северный (жилые от 2,5 м) (К-7).

См. лист открытых вопросов (лист 7, записи К-1, К-2, К-4, К-7).

Примечания

1. Развёртки — вид на стену изнутри помещения, по часовой стрелке; расположение — на схеме листа и на листе 102; размеры — в мм по чистовым поверхностям; отметки — в м от ±0,000; высоты Н — от чистого пола помещения до оси изделия, у декора — до центра.
2. Красные цепочки — привязки электроточек и выводов: по горизонтали от угла чистовых стен, по вертикали от чистого пола, до оси изделия; звенья короче 3 мм на листе вынесены во второй ярус (ближняя к стене цепочка).
3. У знака электроточки: марка (Р — розетка, S — выключатель, Св — светильник, ЭВ — вывод кабеля), ×N — число постов в рамке, гр. — группа щита, Н — высота оси от чистого пола, мм; группы по клавишам выключателя — на листе выключателей.
4. Схема мебели, приборов и декора не является технической документацией для производства мебели; габариты — по паспортам изделий (* — высота не задана в проекте, показана по типовому изделию).
5. Выводы ВК — коды и высоты по листу выводов сантехники; * — высота принята по типовой практике монтажа, окончательно — по паспорту прибора.
6. Облицовка — по сетке швов 2 мм, раскладка от оси стены (треугольник у пола), целые ряды от пола; подрезки — по листу раскладки плитки.
7. Гидроизоляция в 2 слоя, заход на стены 200 мм — до облицовки, с актом скрытых работ и тестом проливом (узел — на листе узлов).
8. Двери скрытого монтажа — полотно в плоскости стены, отделка стены по полотну, плинтус прерывается у короба (узел — на листе узлов).

1000 мм · печать 1:1

Изм.	Кол.уч	Лист	№ док.	Подп.	Дата
Разраб.		Кырлан А.С.			21.10.26
Пров.					
ГИП					
Н. контр.					
Утв.					

ГД-2026-010-АИ

Дом 331 м²

Общая площадь 270,67* м² · * размеры приняты, не замерены (реестр — л. 7, К-1)

Дизайн-проект интерьера

Стадия	Лист	Листов
РП	136	159

Развёртка стены Г. Санузел мастер (пом. 15)

М 1:20

Кырлан Александр Сергеевич

выпуск 18.10.2026 № 9365d64cec · стр. 142 из 197

Развёртки стен А, Б. Спальня 2 (пом. 16)

Спальня 2 (пом. 16) · вид изнутри помещения · размеры в мм, отметки в м

ПРЕДВАРИТЕЛЬНО · не для производства работ · открыто пунктов: 6 (реестр — л. 7)

Развёртка стены А

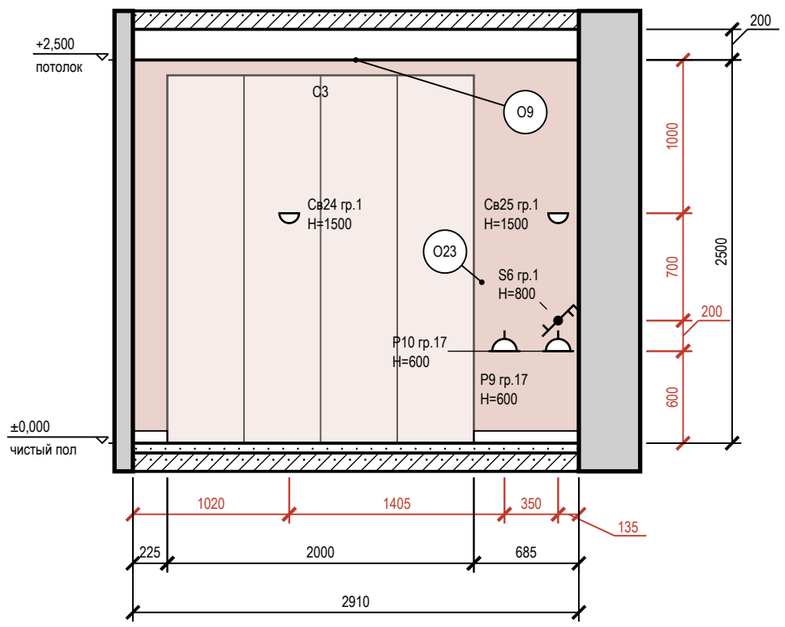

Развёртка стены Б

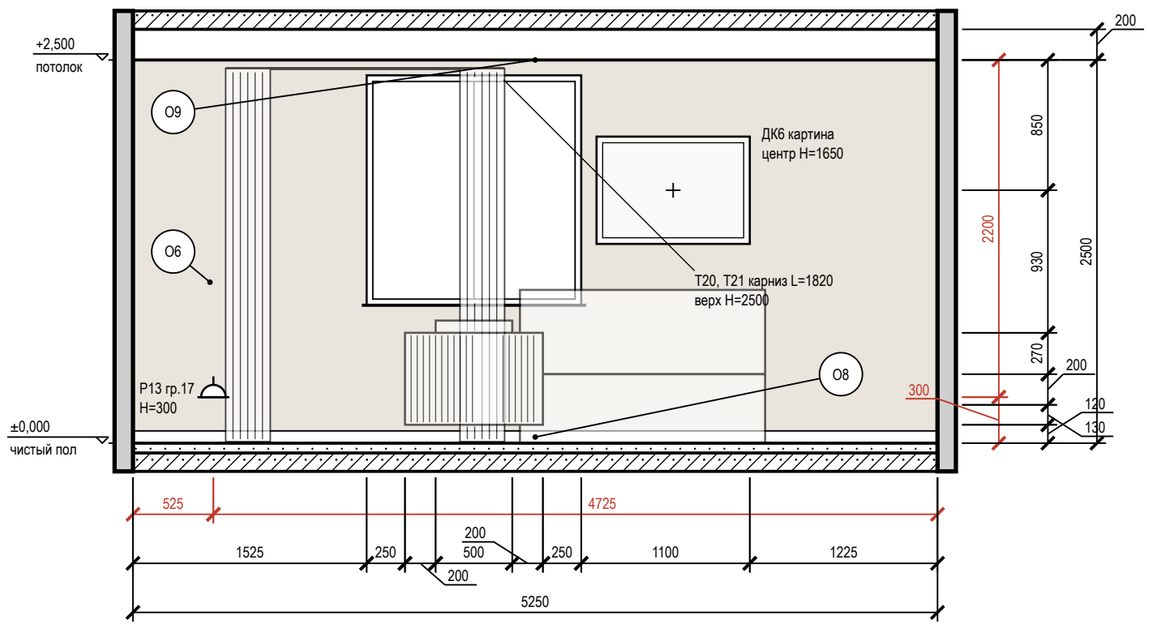

Схема развёрток (М 1:100)

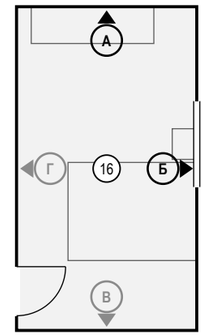

Условные обозначения

- розетка с заземляющим контактом; у знака — марка, ×N постов в рамке, гр. — группа щита, Н — высота оси, мм
- выключатель одноклавишный
- выключатель двухклавишный (флажков — по числу клавиш)
- выключатель с проходной или перекрёстной клавишей (обратный флажок); тип клавиши — в подписи
- светильник настенный (бра), Н — высота оси
- привязки точек и выводов от угла и от пола, мм
- мебель и приборы — фасад по расстановке (условно)
- картина (декор): марка Д, крест — центр, Н — высота центра, мм
- карниз (шина) и шторы в собранном виде: марка Т, длина L, верх Н
- окно: проём, рама, подоконник
- радиатор отопления; марка — по плану отопления
- стены и перекрытия в сечении
- окраска: тон — цвет по коду производителя (условно)
- О1 — марка отделки по реестру отделки альбома
- А — марка развёртки: буква стены, стрелка — взгляд

Ведомость отделки (на листе)

Марка	Поверхность	Материал, изделие	Цвет, код	Кол.
О6	стены	окраска, Farrow & Ball Modern Emulsion, матовая, подготовка Q3	Farrow & Ball No. 226 «Joa's White»	11 м²
О8	плинтус	плинтус МДФ, h 80 мм, аналог: плинтус МДФ под покраску 80×16	Farrow & Ball No. 226 «Joa's White»	6,2 м
О9	потолок	окраска, Tikkurila Anti-Reflex 2, глубокоматовая, подготовка Q3	Little Greene No. 105 «Slaked Lime»	15,5 м²
О23	акцентная стена	окраска, Farrow & Ball Modern Emulsion, матовая, подготовка Q3	Farrow & Ball No. 64 «Red Earth»	7,3 м²

Допущения и предложения на листе

Основа листа: размеры и контуры этажей подобраны проектировщиком по составу помещений и площадям этажей с картинки 470 px (размеры на ней не читаются); обмер и исходный проект — задание (К-1); высоты: 1-й этаж 2800 мм, мансарда 2700 мм (горизонтальная часть) приняты; скаты кровли мансарды приняты по картинке: колено 1200 мм, уклон 45°, конёк вдоль длинной стороны; проект КР — задание (К-2); наружные стены 400 мм, перегородки 120 мм приняты (К-1); разрешённая мощность 15 кВт принята по типовым ТУ для частного дома (К-4); подрайон климата не задан — принят не северный (жилые от 2,5 м) (К-7).

См. лист открытых вопросов (лист 7, записи К-1, К-2, К-4, К-7).

Примечания

1. Развёртки — вид на стену изнутри помещения, по часовой стрелке; расположение — на схеме листа и на листе 102; размеры — в мм по чистовым поверхностям; отметки — в м от ±0,000; высоты Н — от чистого пола помещения до оси изделия, у декора — до центра.
2. Красные цепочки — привязки электроточек и выводов: по горизонтали от угла чистовых стен, по вертикали от чистого пола, до оси изделия; звенья короче 3 мм на листе вынесены во второй ярус (ближняя к стене цепочка).
3. У знака электроточки: марка (Р — розетка, S — выключатель, Св — светильник, ЭВ — вывод кабеля), ×N — число постов в рамке, гр. — группа щита, Н — высота оси от чистого пола, мм; группы по клавишам выключателя — на листе выключателей.
4. Схема мебели, приборов и декора не является технической документацией для производства мебели; габариты — по паспортам изделий.
5. Картины и зеркала крепить к основанию по паспорту изделия (закладные и анкеры — в перечне скрытых работ); крест — ось центра предмета.
6. Карнизы (шины) — по ведомости текстиля декоратора; длина L и верх Н — по развёртке, крепление — до окраски потолка.
7. Потолок на развёртках — по нижнему уровню У2; другие уровни потолка помещения: У1 +2,600.
8. Линии узора (швы плитки, складки штор, рёбра радиаторов) прерываются у знаков и выносок — просвет между линиями не менее 0,7 мм.

1000 мм · печать 1:1

Изм.	Кол.уч	Лист	№ док.	Подп.	Дата
Разраб.		Кырлан А.С.			21.10.26
Пров.					
ГИП					
Н. контр.					
Утв.					

ГД-2026-010-АИ

Дом 331 м²

Общая площадь 270,67* м² · * размеры приняты, не замерены (реестр — л. 7, К-1)

Дизайн-проект интерьера

Стадия	Лист	Листов
РП	137	159

Развёртки стен А, Б. Спальня 2 (пом. 16)

М 1:40

Кырлан Александр Сергеевич

выпуск 18.10.2026 № 9365d64cec · стр. 143 из 197

Развёртки стен В, Г. Спальня 2 (пом. 16)

Спальня 2 (пом. 16) · вид изнутри помещения · размеры в мм, отметки в м

ПРЕДВАРИТЕЛЬНО · не для производства работ · открыто пунктов: 6 (реестр — л. 7)

Развёртка стены В

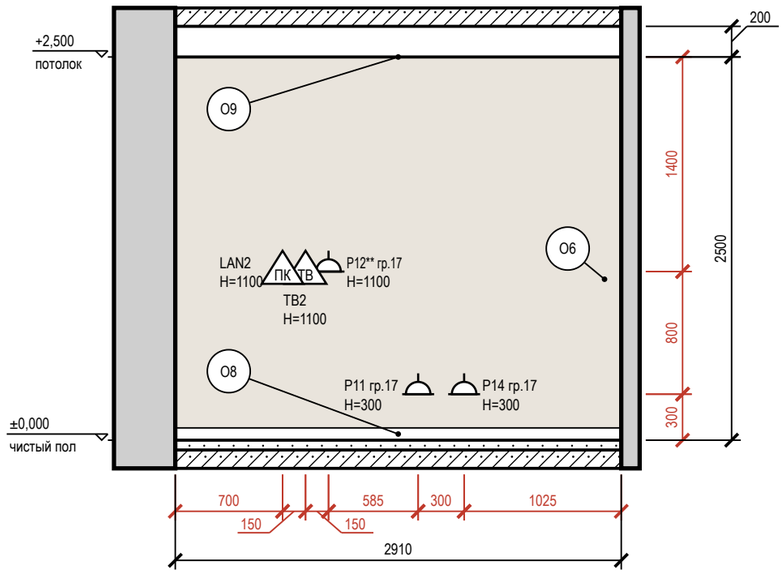

Развёртка стены Г

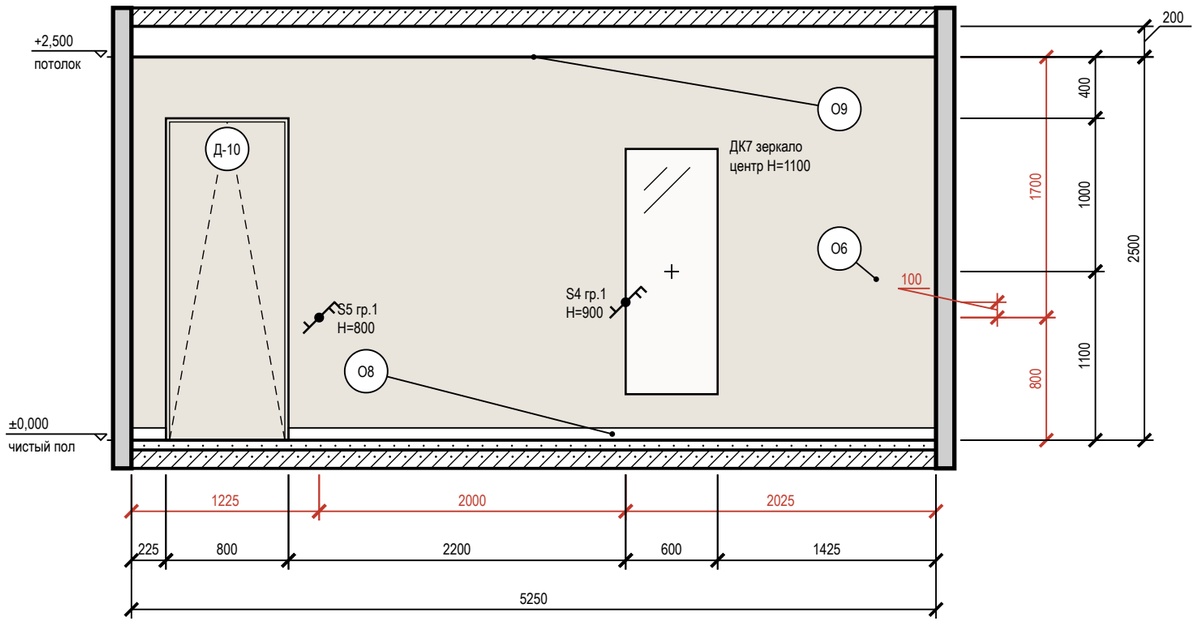

Схема развёрток (М 1:100)

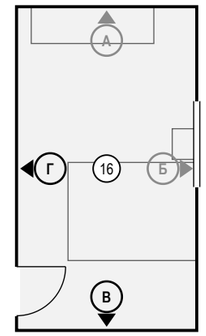

Условные обозначения

- розетка с заземляющим контактом; у знака — марка, ×N постов в рамке, гр. — группа щита, Н — высота оси, мм
- выключатель одноклавишный
- выключатель двухклавишный (флажков — по числу клавиш)
- выключатель с проходной или перекрёстной клавишей (обратный флажок); тип клавиши — в подписи
- ПК — розетка компьютерная RJ45
- ТВ — розетка телевизионная
- привязки точек и выводов от угла и от пола, мм
- мебель и приборы — фасад по расстановке (условно)
- зеркало: марка Д, крест — центр, Н — высота центра, мм
- дверь скрытого монтажа: полотно в плоскости стены (узел — на листе узлов)
- стены и перекрытия в сечении
- окраска: тон — цвет по коду производителя (условно)
- О1 — марка отделки по реестру отделки альбома
- А — марка развёртки: буква стены, стрелка — взгляд

Ведомость отделки (на листе)

Марка	Поверхность	Материал, изделие	Цвет, код	Кол.
О6	стены	окраска, Farrow & Ball Modern Emulsion, матовая, подготовка Q3	Farrow & Ball No. 226 «Joa's White»	18,7 м²
О8	плинтус	плинтус МДФ, h 80 мм, аналог: плинтус МДФ под покраску 80×16	Farrow & Ball No. 226 «Joa's White»	7,4 м
О9	потолок	окраска, Tikkurila Anti-Reflex 2, глубокоматовая, подготовка Q3	Little Greene No. 105 «Slaked Lime»	15,5 м²

Допущения и предложения на листе

Основа листа: размеры и контуры этажей подобраны проектировщиком по составу помещений и площадям этажей с картинки 470 px (размеры на ней не читаются); обмер и исходный проект — задание (К-1); высоты: 1-й этаж 2800 мм, мансарда 2700 мм (горизонтальная часть) приняты; скаты кровли мансарды приняты по картинке: колено 1200 мм, уклон 45°, конёк вдоль длинной стороны; проект КР — задание (К-2); наружные стены 400 мм, перегородки 120 мм приняты (К-1); разрешённая мощность 15 кВт принята по типовым ТУ для частного дома (К-4); подрайон климата не задан — принят не северный (жилые от 2,5 м) (К-7).

Знак «**» — предложение проектировщика, заказчиком не утверждено (согласовать с заказчиком): записи в реестре нет: Р12 — высота 1100 мм выше нормы 1 м (ПУЭ 6.6.30) по назначению: питание ТВ над комодом, в одной зоне с выводами ТВ2 и LAN2.

См. лист открытых вопросов (лист 7, записи К-1, К-2, К-4, К-7).

Примечания

1. Развёртки — вид на стену изнутри помещения, по часовой стрелке; расположение — на схеме листа и на листе 102; размеры — в мм по чистовым поверхностям; отметки — в м от ±0,000; высоты Н — от чистого пола помещения до оси изделия, у декора — до центра.
2. Красные цепочки — привязки электроточек и выводов: по горизонтали от угла чистовых стен, по вертикали от чистого пола, до оси изделия; звенья короче 3 мм на листе вынесены во второй ярус (ближняя к стене цепочка).
3. У знака электроточки: марка (Р — розетка, S — выключатель, Св — светильник, ЭВ — вывод кабеля), ×N — число постов в рамке, гр. — группа щита, Н — высота оси от чистого пола, мм; группы по клавишам выключателя — на листе выключателей.
4. Схема мебели, приборов и декора не является технической документацией для производства мебели; габариты — по паспортам изделий.
5. Картины и зеркала крепить к основанию по паспорту изделия (закладные и анкеры — в перечне скрытых работ); крест — ось центра предмета.
6. Двери скрытого монтажа — полотно в плоскости стены, отделка стены по полотну, плинтус прерывается у короба (узел — на листе узлов).
7. Потолок на развёртках — по нижнему уровню У2; другие уровни потолка помещения: У1 +2,600.

1000 мм · печать 1:1

Изм.	Кол.уч	Лист	№ док.	Подп.	Дата
Разраб.		Кырлан А.С.			21.10.26
Пров.					
ГИП					
Н. контр.					
Утв.					

ГД-2026-010-АИ

Дом 331 м²

Общая площадь 270,67* м² · * размеры приняты, не замерены (реестр — л. 7, К-1)

Дизайн-проект интерьера

Стадия	Лист	Листов
РП	138	159

Развёртки стен В, Г. Спальня 2 (пом. 16)

М 1:40

Кырлан Александр Сергеевич

выпуск 18.10.2026 № 9365d64cec · стр. 144 из 197

Развёртки стен А, Б. Холл мансарды (пом. 17)

Холл мансарды (пом. 17) · вид изнутри помещения · размеры в мм, отметки в м

ПРЕДВАРИТЕЛЬНО · не для производства работ · открыто пунктов: 6 (реестр — л. 7)

Развёртка стены А

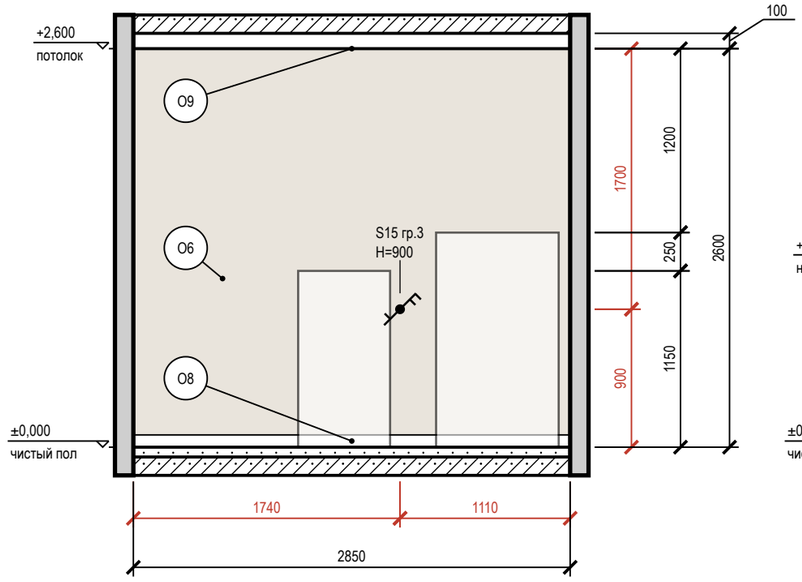

Развёртка стены Б

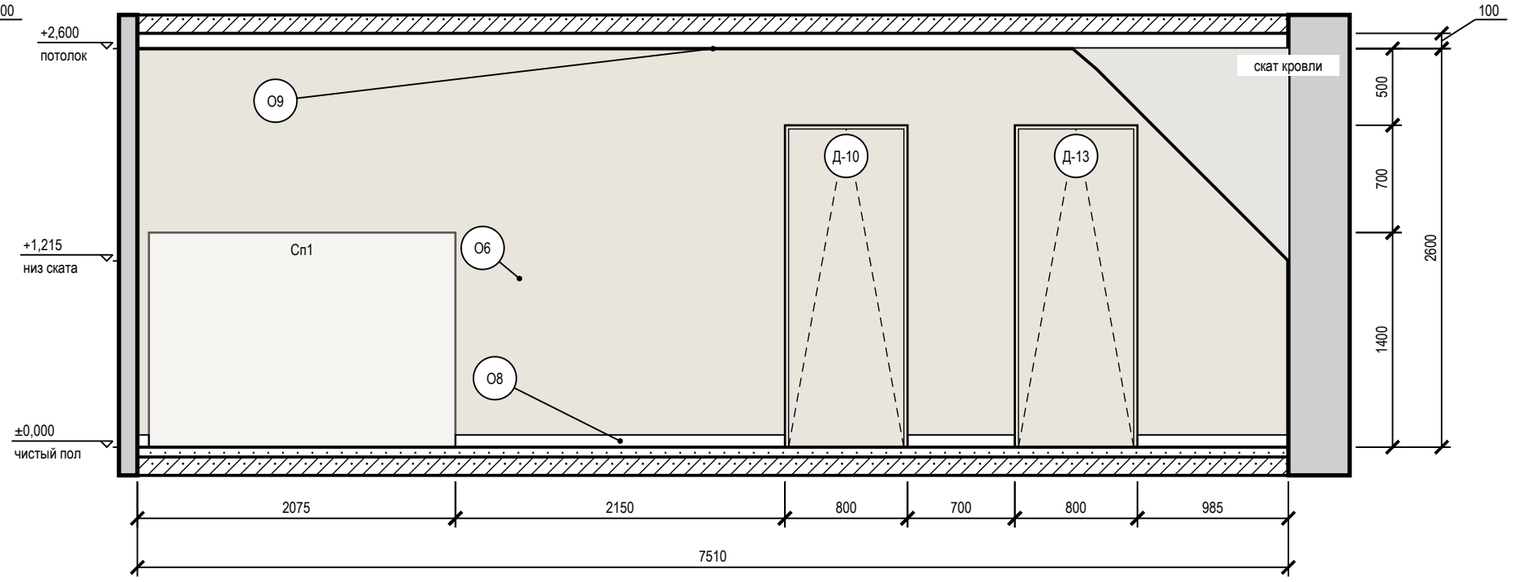

Схема развёрток (М 1:100)

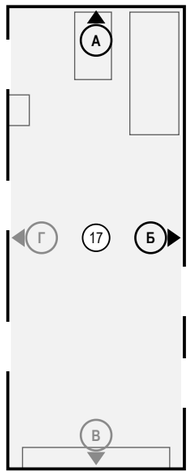

Условные обозначения

- выключатель одноклавишный
- выключатель двухклавишный (флажков — по числу клавиш)
- выключатель с проходной или перекрёстной клавишей (обратный флажок); тип клавиши — в подписи
- привязки точек и выводов от угла и от пола, мм
- мебель и приборы — фасад по расстановке (условно)
- дверь скрытого монтажа: полотно в плоскости стены (узел — на листе узлов)
- стены и перекрытия в сечении
- окраска: тон — цвет по коду производителя (условно)
- О1 — марка отделки по реестру отделки альбома
- А — марка развёртки: буква стены, стрелка — взгляд

Ведомость отделки (на листе)

Марка	Поверхность	Материал, изделие	Цвет, код	Кол.
О6	стены	окраска, Farrow & Ball Modern Emulsion, матовая, подготовка Q3	Farrow & Ball No. 226 «Joa's White»	23,6 м²
О8	плинтус	плинтус МДФ, h 80 мм, аналог: плинтус МДФ под покраску 80×16	Farrow & Ball No. 226 «Joa's White»	6,8 м
О9	потолок	окраска, Tikkurila Anti-Reflex 2, глубокоматовая, подготовка Q3	Little Greene No. 105 «Slaked Lime»	21,7 м²

Допущения и предложения на листе

Основа листа: размеры и контуры этажей подобраны проектировщиком по составу помещений и площадям этажей с картинки 470 px (размеры на ней не читаются); обмер и исходный проект — задание (К-1); высоты: 1-й этаж 2800 мм, мансарда 2700 мм (горизонтальная часть) приняты; скаты кровли мансарды приняты по картинке: колено 1200 мм, уклон 45°, конёк вдоль длинной стороны; проект КР — задание (К-2); наружные стены 400 мм, перегородки 120 мм приняты (К-1); разрешённая мощность 15 кВт принята по типовым ТУ для частного дома (К-4); подрайон климата не задан — принят не северный (жилые от 2,5 м) (К-7).

См. лист открытых вопросов (лист 7, записи К-1, К-2, К-4, К-7).

Примечания

1. Развёртки — вид на стену изнутри помещения, по часовой стрелке; расположение — на схеме листа и на листе 102; размеры — в мм по чистовым поверхностям; отметки — в м от ±0,000; высоты Н — от чистого пола помещения до оси изделия, у декора — до центра.
2. Красные цепочки — привязки электроточек и выводов: по горизонтали от угла чистовых стен, по вертикали от чистого пола, до оси изделия; звенья короче 3 мм на листе вынесены во второй ярус (ближняя к стене цепочка).
3. У знака электроточки: марка (Р — розетка, S — выключатель, Св — светильник, ЭВ — вывод кабеля), ×N — число постов в рамке, гр. — группа щита, Н — высота оси от чистого пола, мм; группы по клавишам выключателя — на листе выключателей.
4. Схема мебели, приборов и декора не является технической документацией для производства мебели; габариты — по паспортам изделий.
5. Двери скрытого монтажа — полотно в плоскости стены, отделка стены по полотну, плинтус прерывается у короба (узел — на листе узлов).

1000 мм · печать 1:1

Изм.	Кол.уч	Лист	№ док.	Подп.	Дата
Разраб.		Кырлан А.С.			21.10.26
Пров.					
ГИП					
Н. контр.					
Утв.					

ГД-2026-010-АИ

Дом 331 м²

Общая площадь 270,67* м² · * размеры приняты, не замерены (реестр — л. 7, К-1)

Дизайн-проект интерьера

Стадия	Лист	Листов
РП	139	159

Развёртки стен А, Б. Холл мансарды (пом. 17)

М 1:40

Кырлан Александр Сергеевич

выпуск 18.10.2026 № 9365d64cec · стр. 145 из 197

Развёртка стены В. Холл мансарды (пом. 17)

Холл мансарды (пом. 17) · вид изнутри помещения · размеры в мм, отметки в м

ПРЕДВАРИТЕЛЬНО · не для производства работ · открыто пунктов: 6 (реестр — л. 7)

Развёртка стены В

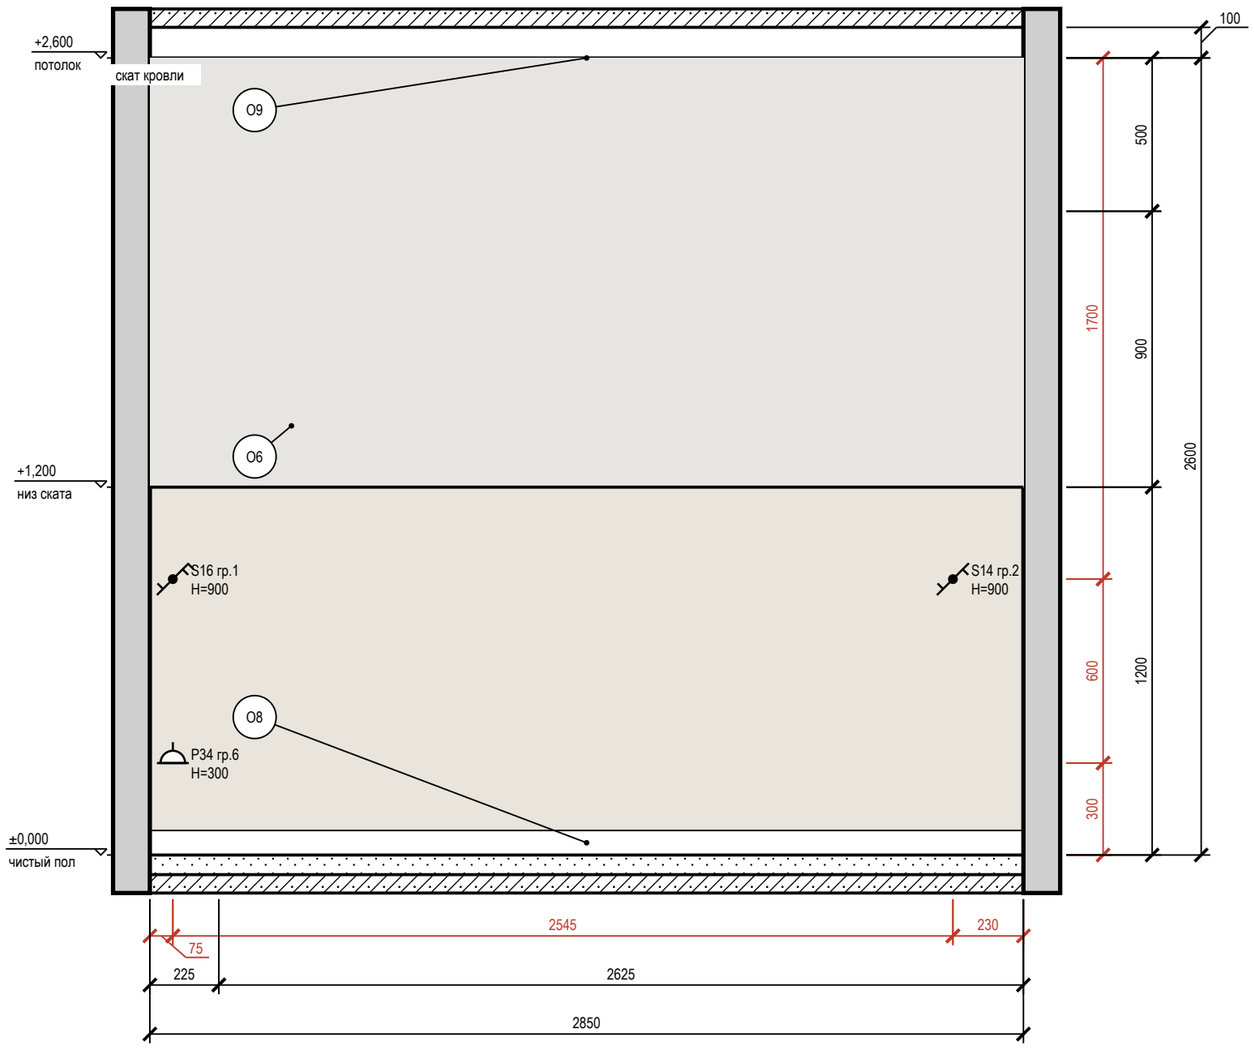

Схема развёрток (М 1:100)

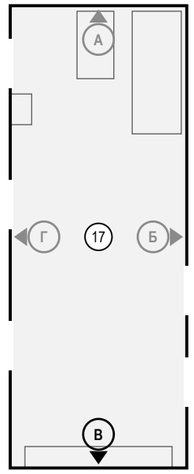

Условные обозначения

- розетка с заземляющим контактом; у знака — марка, ×N постов в рамке, гр. — группа щита, Н — высота оси, мм
- выключатель одноклавишный
- выключатель двухклавишный (флажков — по числу клавиш)
- выключатель с проходной или перекрёстной клавишей (обратный флажок); тип клавиши — в подписи
- привязки точек и выводов от угла и от пола, мм
- мебель и приборы — фасад по расстановке (условно)
- стены и перекрытия в сечении
- окраска: тон — цвет по коду производителя (условно)
- О1 — марка отделки по реестру отделки альбома
- А — марка развёртки: буква стены, стрелка — взгляд

Ведомость отделки (на листе)

Марка	Поверхность	Материал, изделие	Цвет, код	Кол.
О6	стены	окраска, Farrow & Ball Modern Emulsion, матовая, подготовка Q3	Farrow & Ball No. 226 «Joa's White»	7,4 м²
О8	плинтус	плинтус МДФ, h 80 мм, аналог: плинтус МДФ под покраску 80×16	Farrow & Ball No. 226 «Joa's White»	2,9 м
О9	потолок	окраска, Tikkurila Anti-Reflex 2, глубокоматовая, подготовка Q3	Little Greene No. 105 «Slaked Lime»	21,7 м²

Допущения и предложения на листе

Основа листа: размеры и контуры этажей подобраны проектировщиком по составу помещений и площадям этажей с картинки 470 px (размеры на ней не читаются); обмер и исходный проект — задание (К-1); высоты: 1-й этаж 2800 мм, мансарда 2700 мм (горизонтальная часть) приняты; скаты кровли мансарды приняты по картинке: колено 1200 мм, уклон 45°, конёк вдоль длинной стороны; проект КР — задание (К-2); наружные стены 400 мм, перегородки 120 мм приняты (К-1); разрешённая мощность 15 кВт принята по типовым ТУ для частного дома (К-4); подрайон климата не задан — принят не северный (жилые от 2,5 м) (К-7).

См. лист открытых вопросов (лист 7, записи К-1, К-2, К-4, К-7).

Примечания

1. Развёртки — вид на стену изнутри помещения, по часовой стрелке; расположение — на схеме листа и на листе 102; размеры — в мм по чистовым поверхностям; отметки — в м от ±0,000; высоты Н — от чистого пола помещения до оси изделия, у декора — до центра.
2. Красные цепочки — привязки электроточек и выводов: по горизонтали от угла чистовых стен, по вертикали от чистого пола, до оси изделия; звенья короче 3 мм на листе вынесены во второй ярус (ближняя к стене цепочка).
3. У знака электроточки: марка (Р — розетка, S — выключатель, Св — светильник, ЭВ — вывод кабеля), ×N — число постов в рамке, гр. — группа щита, Н — высота оси от чистого пола, мм; группы по клавишам выключателя — на листе выключателей.
4. Схема мебели, приборов и декора не является технической документацией для производства мебели; габариты — по паспортам изделий (* — высота не задана в проекте, показана по типовому изделию).

1000 мм · печать 1:1

Изм.	Кол.уч	Лист	№ док.	Подп.	Дата
Разраб.		Кырлан А.С.			21.10.26
Пров.					
ГИП					
Н. контр.					
Утв.					

ГД-2026-010-АИ

Дом 331 м²

Общая площадь 270,67* м² · * размеры приняты, не замерены (реестр — л. 7, К-1)

Дизайн-проект интерьера

Стадия	Лист	Листов
РП	140	159

Развёртка стены В. Холл мансарды (пом. 17)

М 1:20

Кырлан Александр Сергеевич

выпуск 18.10.2026 № 9365d64cec · стр. 146 из 197

Развёртка стены Г. Холл мансарды (пом. 17)

Холл мансарды (пом. 17) · вид изнутри помещения · размеры в мм, отметки в м

ПРЕДВАРИТЕЛЬНО · не для производства работ · открыто пунктов: 6 (реестр — л. 7)

Развёртка стены Г

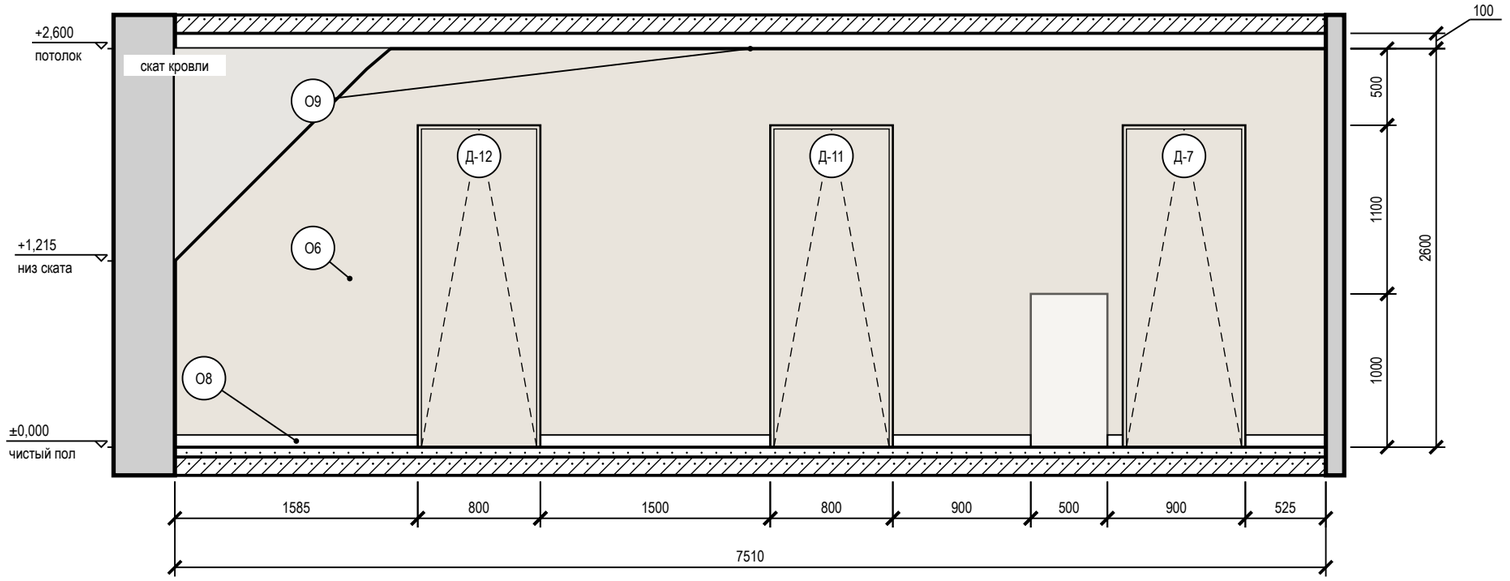

Схема развёрток (М 1:100)

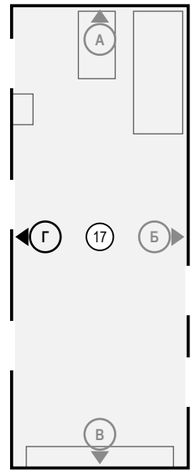

Условные обозначения

- привязки точек и выводов от угла и от пола, мм
- мебель и приборы — фасад по расстановке (условно)
- дверь скрытого монтажа: полотно в плоскости стены (узел — на листе узлов)
- стены и перекрытия в сечении
- окраска: тон — цвет по коду производителя (условно)
- О1 — марка отделки по реестру отделки альбома
- А — марка развёртки: буква стены, стрелка — взгляд

Ведомость отделки (на листе)

Марка	Поверхность	Материал, изделие	Цвет, код	Кол.
О6	стены	окраска, Farrow & Ball Modern Emulsion, матовая, подготовка Q3	Farrow & Ball No. 226 «Joa's White»	14,5 м²
О8	плинтус	плинтус МДФ, h 80 мм, аналог: плинтус МДФ под покраску 80×16	Farrow & Ball No. 226 «Joa's White»	4,6 м
О9	потолок	окраска, Tikkurila Anti-Reflex 2, глубокоматовая, подготовка Q3	Little Greene No. 105 «Slaked Lime»	21,7 м²

Допущения и предложения на листе

Основа листа: размеры и контуры этажей подобраны проектировщиком по составу помещений и площадям этажей с картинки 470 px (размеры на ней не читаются); обмер и исходный проект — задание (К-1); высоты: 1-й этаж 2800 мм, мансарда 2700 мм (горизонтальная часть) приняты; скаты кровли мансарды приняты по картинке: колено 1200 мм, уклон 45°, конёк вдоль длинной стороны; проект КР — задание (К-2); наружные стены 400 мм, перегородки 120 мм приняты (К-1); разрешённая мощность 15 кВт принята по типовым ТУ для частного дома (К-4); подрайон климата не задан — принят не северный (жилые от 2,5 м) (К-7).

См. лист открытых вопросов (лист 7, записи К-1, К-2, К-4, К-7).

Примечания

1. Развёртки — вид на стену изнутри помещения, по часовой стрелке; расположение — на схеме листа и на листе 102; размеры — в мм по чистовым поверхностям; отметки — в м от ±0,000; высоты Н — от чистого пола помещения до оси изделия, у декора — до центра.
2. Красные цепочки — привязки электроточек и выводов: по горизонтали от угла чистовых стен, по вертикали от чистого пола, до оси изделия; звенья короче 3 мм на листе вынесены во второй ярус (ближняя к стене цепочка).
3. У знака электроточки: марка (Р — розетка, S — выключатель, Св — светильник, ЭВ — вывод кабеля), ×N — число постов в рамке, гр. — группа щита, Н — высота оси от чистого пола, мм; группы по клавишам выключателя — на листе выключателей.
4. Схема мебели, приборов и декора не является технической документацией для производства мебели; габариты — по паспортам изделий.
5. Двери скрытого монтажа — полотно в плоскости стены, отделка стены по полотну, плинтус прерывается у короба (узел — на листе узлов).

1000 мм · печать 1:1

Изм.	Кол.уч	Лист	№ док.	Подп.	Дата
Разраб.		Кырлан А.С.			21.10.26
Пров.					
ГИП					
Н. контр.					
Утв.					

ГД-2026-010-АИ

Дом 331 м²

Общая площадь 270,67* м² · * размеры приняты, не замерены (реестр — л. 7, К-1)

Дизайн-проект интерьера

Стадия	Лист	Листов
РП	141	159

Развёртка стены Г. Холл мансарды (пом. 17)

М 1:40

Кырлан Александр Сергеевич

выпуск 18.10.2026 № 9365d64cec · стр. 147 из 197

Развёртки стен А, Б. Спальня 3 (пом. 18)

Спальня 3 (пом. 18) · вид изнутри помещения · размеры в мм, отметки в м

ПРЕДВАРИТЕЛЬНО · не для производства работ · открыто пунктов: 6 (реестр — л. 7)

Развёртка стены А

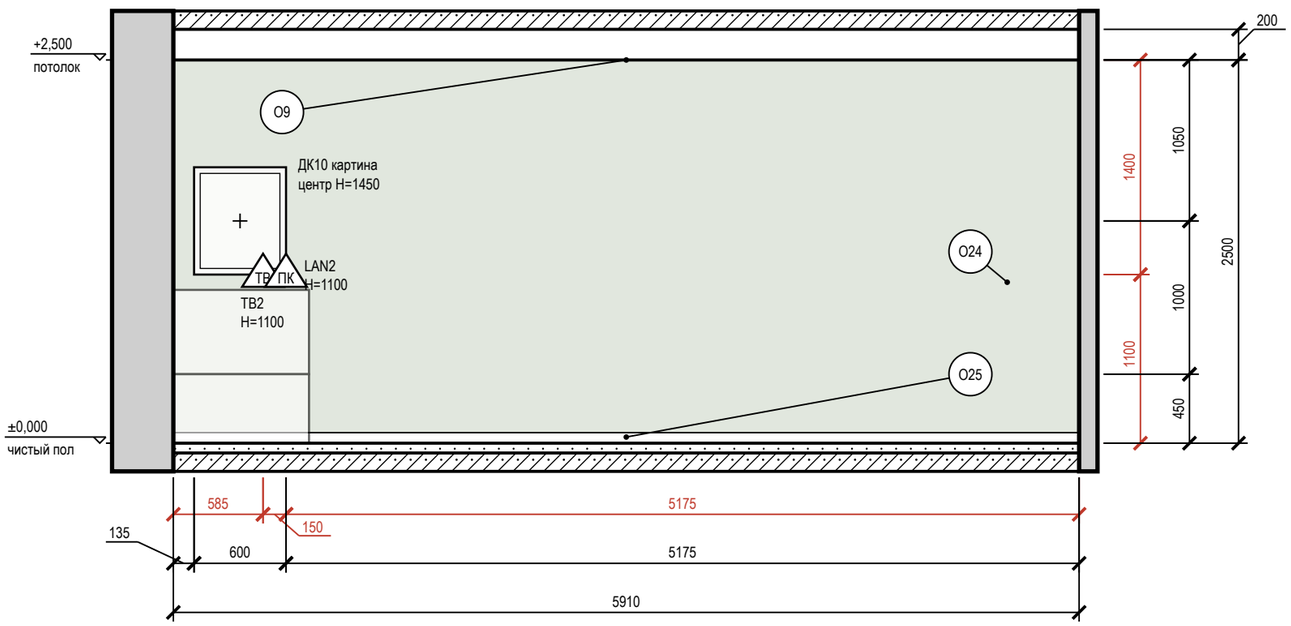

Развёртка стены Б

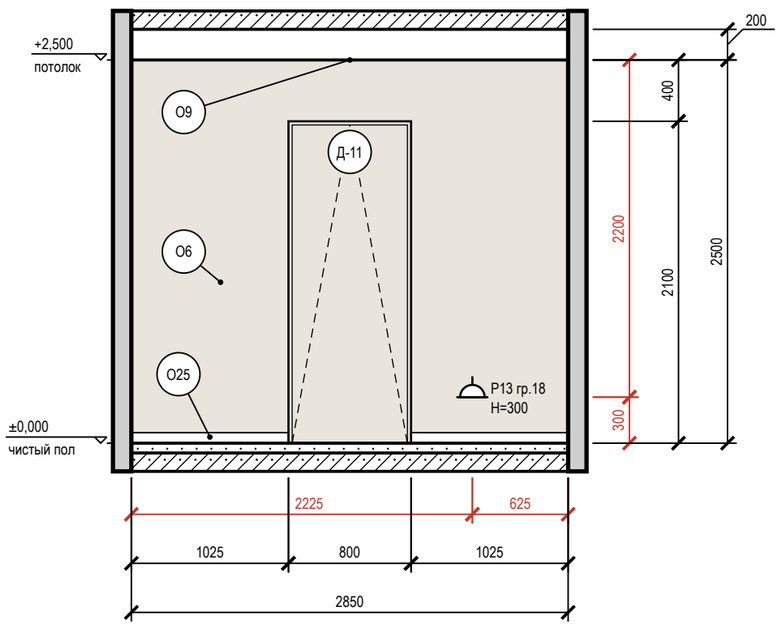

Схема развёрток (М 1:100)

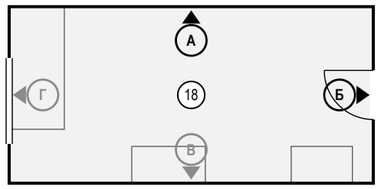

Условные обозначения

- розетка с заземляющим контактом; у знака — марка, ×N постов в рамке, гр. — группа щита, Н — высота оси, мм
- ПК — розетка компьютерная RJ45
- ТВ — розетка телевизионная
- привязки точек и выводов от угла и от пола, мм
- мебель и приборы — фасад по расстановке (условно)
- картина (декор): марка Д, крест — центр, Н — высота центра, мм
- дверь скрытого монтажа: полотно в плоскости стены (узел — на листе узлов)
- стены и перекрытия в сечении
- окраска: тон — цвет по коду производителя (условно)
- О1 — марка отделки по реестру отделки альбома
- А — марка развёртки: буква стены, стрелка — взгляд

Ведомость отделки (на листе)

Марка	Поверхность	Материал, изделие	Цвет, код	Кол.
О6	стены	окраска, Farrow & Ball Modern Emulsion, матовая, подготовка Q3	Farrow & Ball No. 226 «Joa's White»	5,4 м²
О9	потолок	окраска, Tikkurila Anti-Reflex 2, глубокоматовая, подготовка Q3	Little Greene No. 105 «Slaked Lime»	17,1 м²
О24	акцентная стена	окраска, Farrow & Ball Modern Emulsion, матовая, подготовка Q3	NCS S 3020-G30Y «S 3020-G30Y»	14,8 м²
О25	плинтус	плинтус МДФ, Orac Decor Contour (Luxxus), h 69 мм, SX165	Farrow & Ball No. 226 «Joa's White»	8 м

Допущения и предложения на листе

Основа листа: размеры и контуры этажей подобраны проектировщиком по составу помещений и площадям этажей с картинки 470 px (размеры на ней не читаются); обмер и исходный проект — задание (К-1); высоты: 1-й этаж 2800 мм, мансарда 2700 мм (горизонтальная часть) приняты; скаты кровли мансарды приняты по картинке: колено 1200 мм, уклон 45°, конёк вдоль длинной стороны; проект КР — задание (К-2); наружные стены 400 мм, перегородки 120 мм приняты (К-1); разрешённая мощность 15 кВт принята по типовым ТУ для частного дома (К-4); подрайон климата не задан — принят не северный (жилые от 2,5 м) (К-7).

См. лист открытых вопросов (лист 7, записи К-1, К-2, К-4, К-7).

Примечания

1. Развёртки — вид на стену изнутри помещения, по часовой стрелке; расположение — на схеме листа и на листе 102; размеры — в мм по чистовым поверхностям; отметки — в м от ±0,000; высоты Н — от чистого пола помещения до оси изделия, у декора — до центра.
2. Красные цепочки — привязки электроточек и выводов: по горизонтали от угла чистовых стен, по вертикали от чистого пола, до оси изделия; звенья короче 3 мм на листе вынесены во второй ярус (ближняя к стене цепочка).
3. У знака электроточки: марка (Р — розетка, S — выключатель, Св — светильник, ЭВ — вывод кабеля), ×N — число постов в рамке, гр. — группа щита, Н — высота оси от чистого пола, мм; группы по клавишам выключателя — на листе выключателей.
4. Схема мебели, приборов и декора не является технической документацией для производства мебели; габариты — по паспортам изделий.
5. Картины и зеркала крепить к основанию по паспорту изделия (закладные и анкеры — в перечне скрытых работ); крест — ось центра предмета.
6. Двери скрытого монтажа — полотно в плоскости стены, отделка стены по полотну, плинтус прерывается у короба (узел — на листе узлов).
7. Потолок на развёртках — по нижнему уровню У1; другие уровни потолка помещения: У2 +2,600.

1000 мм · печать 1:1

Изм.	Кол.уч	Лист	№ док.	Подп.	Дата
Разраб.		Кырлан А.С.			21.10.26
Пров.					
ГИП					
Н. контр.					
Утв.					

ГД-2026-010-АИ

Дом 331 м²

Общая площадь 270,67* м² · * размеры приняты, не замерены (реестр — л. 7, К-1)

Дизайн-проект интерьера

Стадия	Лист	Листов
РП	142	159

Развёртки стен А, Б. Спальня 3 (пом. 18)

М 1:40

Кырлан Александр Сергеевич

выпуск 18.10.2026 № 9365d64cec · стр. 148 из 197

Развёртки стен В, Г. Спальня 3 (пом. 18)

Спальня 3 (пом. 18) · вид изнутри помещения · размеры в мм, отметки в м

ПРЕДВАРИТЕЛЬНО · не для производства работ · открыто пунктов: 6 (реестр — л. 7)

Развёртка стены В

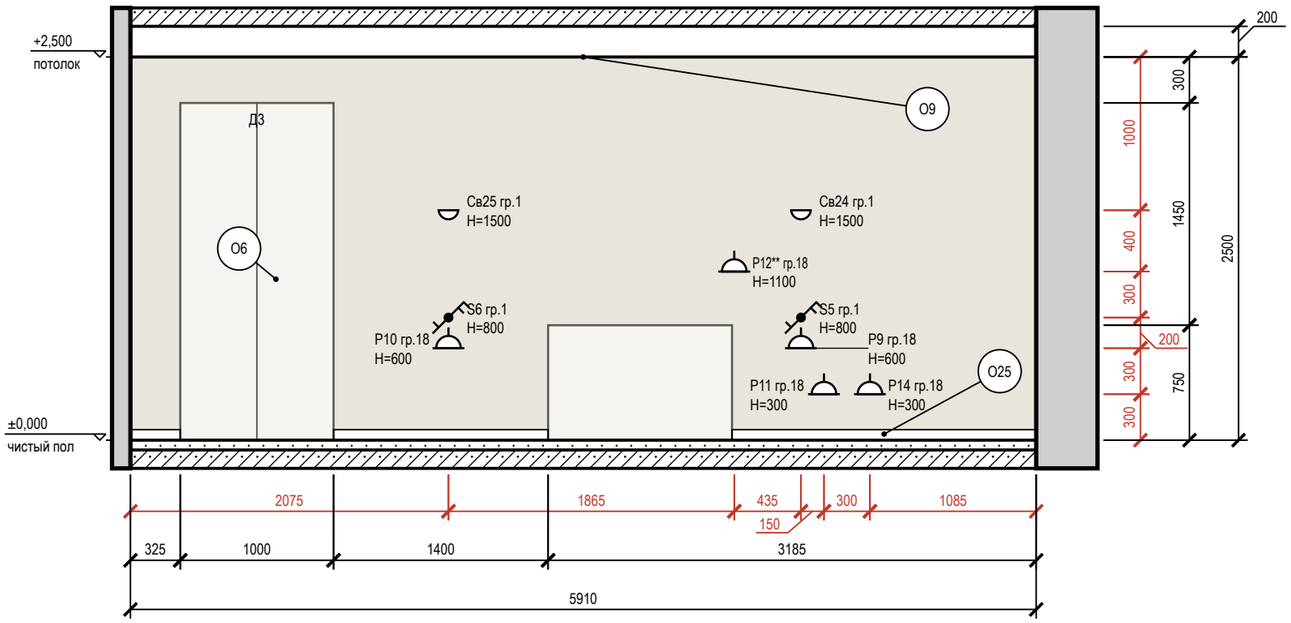

Развёртка стены Г

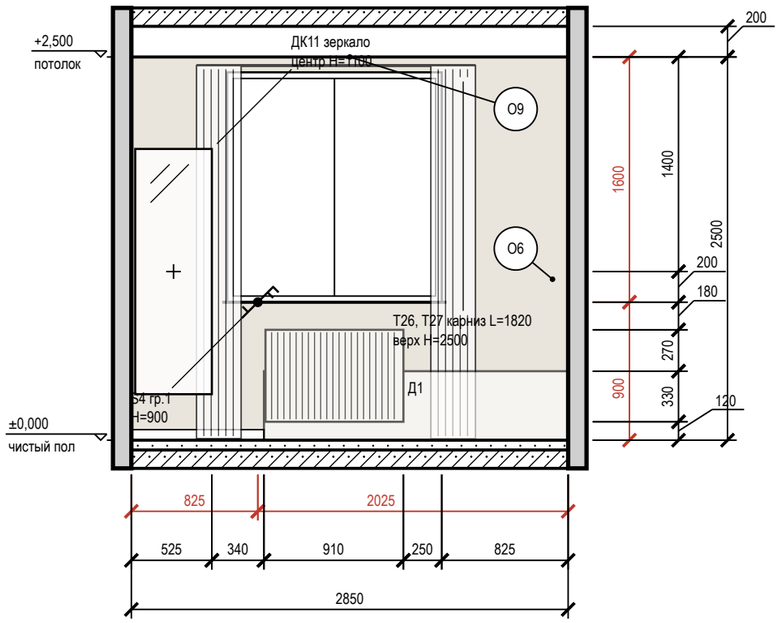

Схема развёрток (М 1:100)

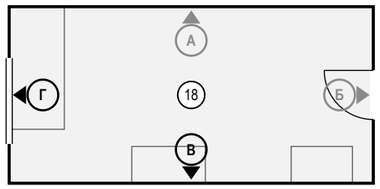

Условные обозначения

- розетка с заземляющим контактом; у знака — марка, ×N постов в рамке, гр. — группа щита, H — высота оси, мм
- выключатель одноклавишный
- выключатель двухклавишный (флажков — по числу клавиш)
- выключатель с проходной или перекрёстной клавишей (обратный флажок); тип клавиши — в подписи
- светильник настенный (бра), H — высота оси
- привязки точек и выводов от угла и от пола, мм
- мебель и приборы — фасад по расстановке (условно)
- зеркало: марка Д, крест — центр, H — высота центра, мм
- карниз (шина) и шторы в собранном виде: марка Т, длина L, верх H
- окно: проём, рама, подоконник
- радиатор отопления; марка — по плану отопления
- стены и перекрытия в сечении
- окраска: тон — цвет по коду производителя (условно)
- О1 — марка отделки по реестру отделки альбома
- А — марка развёртки: буква стены, стрелка — взгляд

Ведомость отделки (на листе)

Марка	Поверхность	Материал, изделие	Цвет, код	Кол.
О6	стены	окраска, Farrow & Ball Modern Emulsion, матовая, подготовка Q3	Farrow & Ball No. 226 «Joa's White»	19,8 м²
О9	потолок	окраска, Tikkurila Anti-Reflex 2, глубокоматовая, подготовка Q3	Little Greene No. 105 «Slaked Lime»	17,1 м²
О25	плинтус	плинтус МДФ, Orac Decor Contour (Luxxus), h 69 мм, SX165	Farrow & Ball No. 226 «Joa's White»	4,6 м

Допущения и предложения на листе

Основа листа: размеры и контуры этажей подобраны проектировщиком по составу помещений и площадям этажей с картинки 470 px (размеры на ней не читаются); обмер и исходный проект — задание (К-1); высоты: 1-й этаж 2800 мм, мансарда 2700 мм (горизонтальная часть) приняты; скаты кровли мансарды приняты по картинке: колено 1200 мм, уклон 45°, конёк вдоль длинной стороны; проект КР — задание (К-2); наружные стены 400 мм, перегородки 120 мм приняты (К-1); разрешённая мощность 15 кВт принята по типовым ТУ для частного дома (К-4); подрайон климата не задан — принят не северный (жилые от 2,5 м) (К-7).

Знак «**» — предложение проектировщика, заказчиком не утверждено (согласовать с заказчиком): записи в реестре нет: Р12 — высота 1100 мм выше нормы 1 м (ПУЭ 6.6.30) по назначению: питание ТВ над комодом, в одной зоне с выводами ТВ2 и LAN2.

См. лист открытых вопросов (лист 7, записи К-1, К-2, К-4, К-7).

Примечания

1. Развёртки — вид на стену изнутри помещения, по часовой стрелке; расположение — на схеме листа и на листе 102; размеры — в мм по чистовым поверхностям; отметки — в м от ±0,000; высоты H — от чистого пола помещения до оси изделия, у декора — до центра.
2. Красные цепочки — привязки электроточек и выводов: по горизонтали от угла чистовых стен, по вертикали от чистого пола, до оси изделия; звенья короче 3 мм на листе вынесены во второй ярус (ближняя к стене цепочка).
3. У знака электроточки: марка (Р — розетка, S — выключатель, Св — светильник, ЭВ — вывод кабеля), ×N — число постов в рамке, гр. — группа щита, H — высота оси от чистого пола, мм; группы по клавишам выключателя — на листе выключателей.
4. Схема мебели, приборов и декора не является технической документацией для производства мебели; габариты — по паспортам изделий.
5. Картины и зеркала крепить к основанию по паспорту изделия (закладные и анкеры — в перечне скрытых работ); крест — ось центра предмета.
6. Карнизы (шины) — по ведомости текстиля декоратора; длина L и верх H — по развёртке, крепление — до окраски потолка.
7. Потолок на развёртках — по нижнему уровню У1; другие уровни потолка помещения: У2 +2,600.
8. Линии узора (швы плитки, складки штор, рёбра радиаторов) прерываются у знаков и выносок — просвет между линиями не менее 0,7 мм.

1000 мм · печать 1:1

Изм.	Кол.уч	Лист	№ док.	Подп.	Дата
Разраб.		Кырлан А.С.			21.10.26
Пров.					
ГИП					
Н. контр.					
Утв.					

ГД-2026-010-АИ

Дом 331 м²

Общая площадь 270,67* м² · * размеры приняты, не замерены (реестр — л. 7, К-1)

Дизайн-проект интерьера

Стадия	Лист	Листов
РП	143	159

Развёртки стен В, Г. Спальня 3 (пом. 18)

М 1:40

Кырлан Александр Сергеевич

выпуск 18.10.2026 № 9365d64cec · стр. 149 из 197

Развёртки стен А, Б. Спальня 4 (пом. 19)

Спальня 4 (пом. 19) · вид изнутри помещения · размеры в мм, отметки в м

ПРЕДВАРИТЕЛЬНО · не для производства работ · открыто пунктов: 6 (реестр — л. 7)

Развёртка стены А

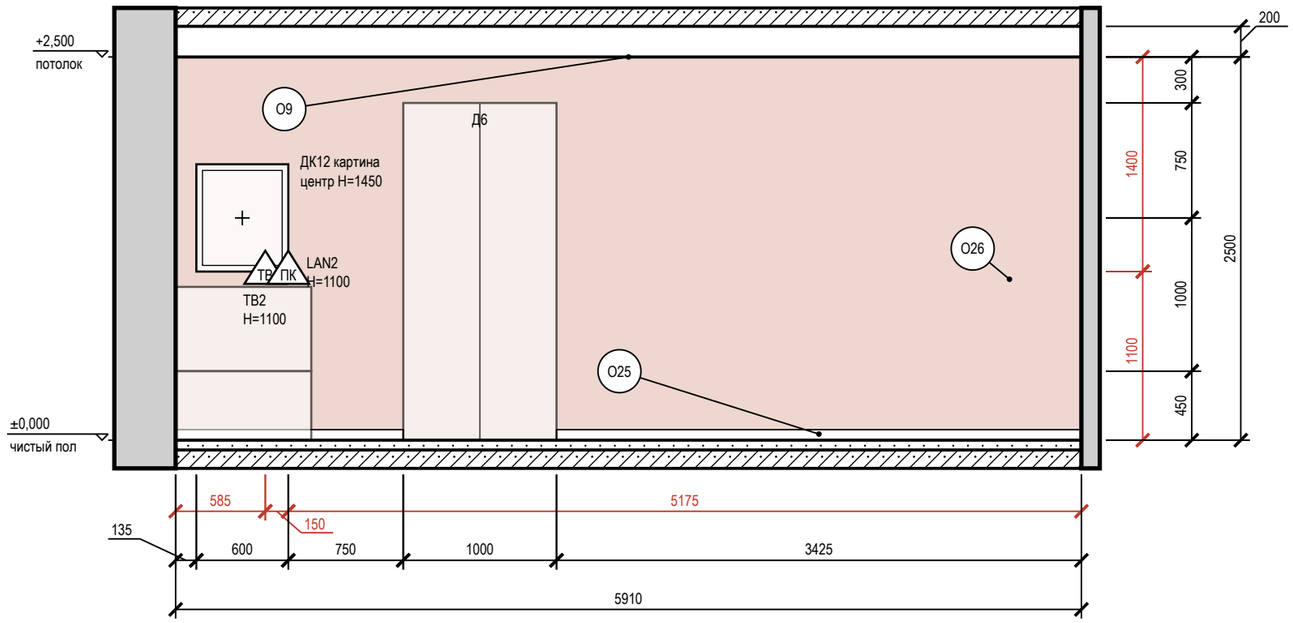

Развёртка стены Б

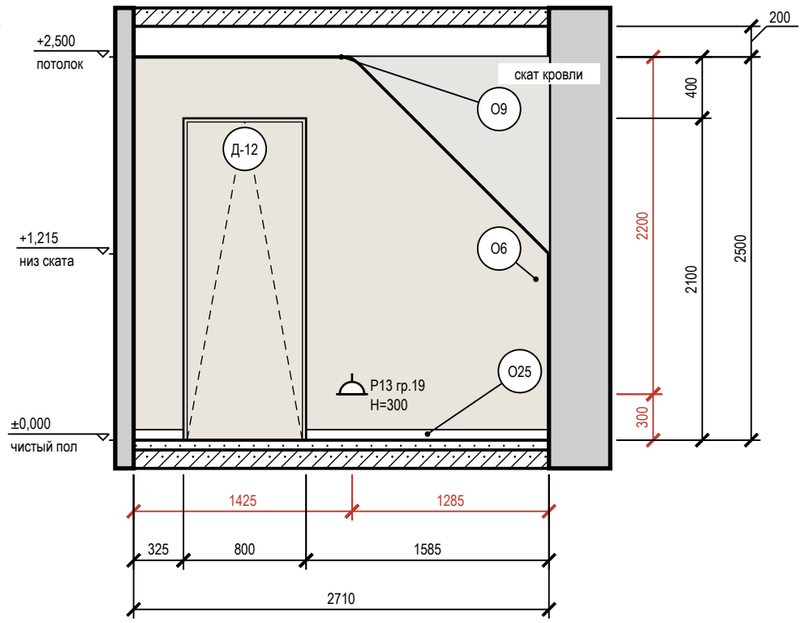

Схема развёрток (М 1:100)

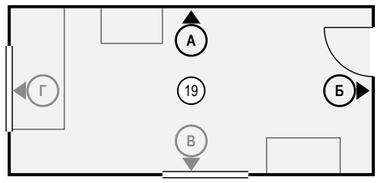

Условные обозначения

- розетка с заземляющим контактом; у знака — марка, ×N постов в рамке, гр. — группа щита, Н — высота оси, мм
- ПК — розетка компьютерная RJ45
- ТВ — розетка телевизионная
- привязки точек и выводов от угла и от пола, мм
- мебель и приборы — фасад по расстановке (условно)
- картина (декор): марка Д, крест — центр, Н — высота центра, мм
- дверь скрытого монтажа: полотно в плоскости стены (узел — на листе узлов)
- стены и перекрытия в сечении
- окраска: тон — цвет по коду производителя (условно)
- О1 — марка отделки по реестру отделки альбома
- А — марка развёртки: буква стены, стрелка — взгляд

Ведомость отделки (на листе)

Марка	Поверхность	Материал, изделие	Цвет, код	Кол.
О6	стены	окраска, Farrow & Ball Modern Emulsion, матовая, подготовка Q3	Farrow & Ball No. 226 «Joa's White»	5,1 м²
О9	потолок	окраска, Tikkurila Anti-Reflex 2, глубокоматовая, подготовка Q3	Little Greene No. 105 «Slaked Lime»	16,3 м²
О25	плинтус	плинтус МДФ, Orac Decor Contour (Luxxus), h 69 мм, SX165	Farrow & Ball No. 226 «Joa's White»	6,8 м
О26	акцентная стена	окраска, Farrow & Ball Modern Emulsion, матовая, подготовка Q3	NCS S 3040-Y70R «S 3040-Y70R»	14,8 м²

Допущения и предложения на листе

Основа листа: размеры и контуры этажей подобраны проектировщиком по составу помещений и площадям этажей с картинки 470 px (размеры на ней не читаются); обмер и исходный проект — задание (К-1); высоты: 1-й этаж 2800 мм, мансарда 2700 мм (горизонтальная часть) приняты; скаты кровли мансарды приняты по картинке: колено 1200 мм, уклон 45°, конёк вдоль длинной стороны; проект КР — задание (К-2); наружные стены 400 мм, перегородки 120 мм приняты (К-1); разрешённая мощность 15 кВт принята по типовым ТУ для частного дома (К-4); подрайон климата не задан — принят не северный (жилые от 2,5 м) (К-7).

См. лист открытых вопросов (лист 7, записи К-1, К-2, К-4, К-7).

Примечания

1. Развёртки — вид на стену изнутри помещения, по часовой стрелке; расположение — на схеме листа и на листе 102; размеры — в мм по чистовым поверхностям; отметки — в м от ±0,000; высоты Н — от чистого пола помещения до оси изделия, у декора — до центра.
2. Красные цепочки — привязки электроточек и выводов: по горизонтали от угла чистовых стен, по вертикали от чистого пола, до оси изделия; звенья короче 3 мм на листе вынесены во второй ярус (ближняя к стене цепочка).
3. У знака электроточки: марка (Р — розетка, S — выключатель, Св — светильник, ЭВ — вывод кабеля), ×N — число постов в рамке, гр. — группа щита, Н — высота оси от чистого пола, мм; группы по клавишам выключателя — на листе выключателей.
4. Схема мебели, приборов и декора не является технической документацией для производства мебели; габариты — по паспортам изделий.
5. Картины и зеркала крепить к основанию по паспорту изделия (закладные и анкеры — в перечне скрытых работ); крест — ось центра предмета.
6. Двери скрытого монтажа — полотно в плоскости стены, отделка стены по полотну, плинтус прерывается у короба (узел — на листе узлов).
7. Потолок на развёртках — по нижнему уровню У1; другие уровни потолка помещения: У2 +2,600.

1000 мм · печать 1:1

Изм.	Кол.уч	Лист	№ док.	Подп.	Дата
Разраб.		Кырлан А.С.			21.10.26
Пров.					
ГИП					
Н. контр.					
Утв.					

ГД-2026-010-АИ

Дом 331 м²

Общая площадь 270,67* м² · * размеры приняты, не замерены (реестр — л. 7, К-1)

Дизайн-проект интерьера

Стадия	Лист	Листов
РП	144	159

Развёртки стен А, Б. Спальня 4 (пом. 19)

М 1:40

Кырлан Александр Сергеевич

выпуск 18.10.2026 № 9365d64cec · стр. 150 из 197

Развёртки стен В, Г. Спальня 4 (пом. 19)

Спальня 4 (пом. 19) · вид изнутри помещения · размеры в мм, отметки в м

ПРЕДВАРИТЕЛЬНО · не для производства работ · открыто пунктов: 6 (реестр — л. 7)

Развёртка стены В

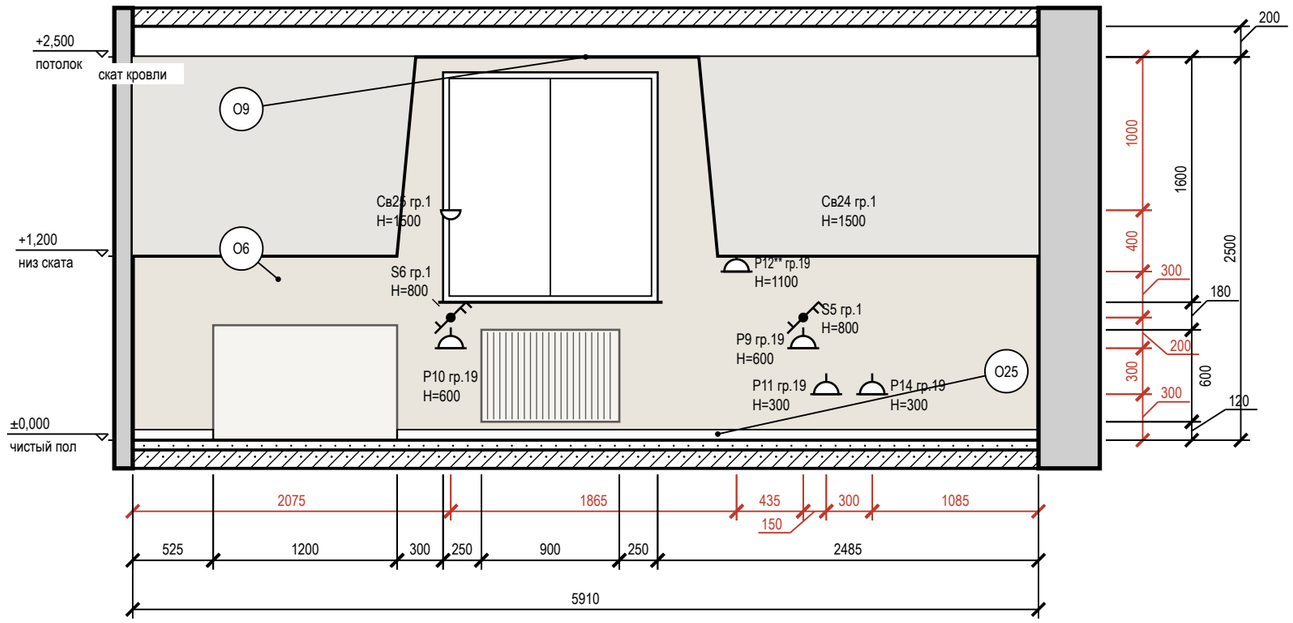

Развёртка стены Г

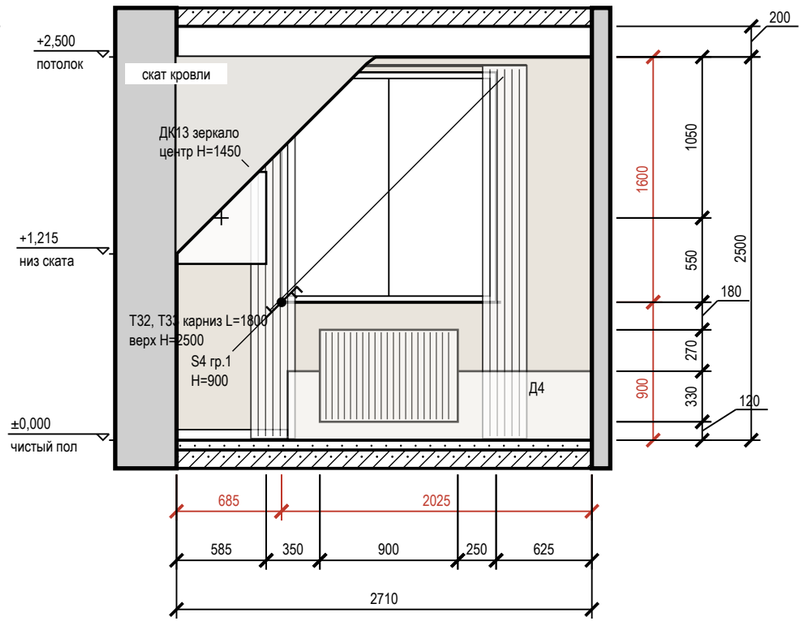

Схема развёрток (М 1:100)

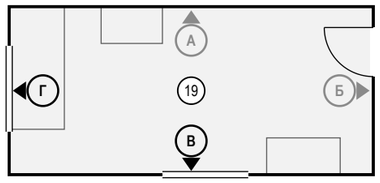

Условные обозначения

- розетка с заземляющим контактом; у знака — марка, ×N постов в рамке, гр. — группа щита, H — высота оси, мм
- выключатель одноклавишный
- выключатель двухклавишный (флажков — по числу клавиш)
- выключатель с проходной или перекрёстной клавишей (обратный флажок); тип клавиши — в подписи
- светильник настенный (бра), H — высота оси
- привязки точек и выводов от угла и от пола, мм
- мебель и приборы — фасад по расстановке (условно)
- зеркало: марка Д, крест — центр, H — высота центра, мм
- карниз (шина) и шторы в собранном виде: марка Т, длина L, верх H
- окно: проём, рама, подоконник
- радиатор отопления; марка — по плану отопления
- стены и перекрытия в сечении
- окраска: тон — цвет по коду производителя (условно)
- О1 — марка отделки по реестру отделки альбома
- А — марка развёртки: буква стены, стрелка — взгляд

Ведомость отделки (на листе)

Марка	Поверхность	Материал, изделие	Цвет, код	Кол.
О6	стены	окраска, Farrow & Ball Modern Emulsion, матовая, подготовка Q3	Farrow & Ball No. 226 «Joa's White»	17,4 м²
О9	потолок	окраска, Tikkurila Anti-Reflex 2, глубокоматовая, подготовка Q3	Little Greene No. 105 «Slaked Lime»	16,3 м²
О25	плинтус	плинтус МДФ, Orac Decor Contour (Luxxus), h 69 мм, SX165	Farrow & Ball No. 226 «Joa's White»	5,4 м

Допущения и предложения на листе

Основа листа: размеры и контуры этажей подобраны проектировщиком по составу помещений и площадям этажей с картинки 470 px (размеры на ней не читаются); обмер и исходный проект — задание (К-1); высоты: 1-й этаж 2800 мм, мансарда 2700 мм (горизонтальная часть) приняты; скаты кровли мансарды приняты по картинке: колено 1200 мм, уклон 45°, конёк вдоль длинной стороны; проект КР — задание (К-2); наружные стены 400 мм, перегородки 120 мм приняты (К-1); разрешённая мощность 15 кВт принята по типовым ТУ для частного дома (К-4); подрайон климата не задан — принят не северный (жилые от 2,5 м) (К-7).

Знак «**» — предложение проектировщика, заказчиком не утверждено (согласовать с заказчиком): записи в реестре нет: Р12 — высота 1100 мм выше нормы 1 м (ПУЭ 6.6.30) по назначению: питание ТВ над комодом, в одной зоне с выводами ТВ2 и LAN2.

См. лист открытых вопросов (лист 7, записи К-1, К-2, К-4, К-7).

Примечания

1. Развёртки — вид на стену изнутри помещения, по часовой стрелке; расположение — на схеме листа и на листе 102; размеры — в мм по чистовым поверхностям; отметки — в м от ±0,000; высоты H — от чистого пола помещения до оси изделия, у декора — до центра.
2. Красные цепочки — привязки электроточек и выводов: по горизонтали от угла чистовых стен, по вертикали от чистого пола, до оси изделия; звенья короче 3 мм на листе вынесены во второй ярус (ближняя к стене цепочка).
3. У знака электроточки: марка (Р — розетка, S — выключатель, Св — светильник, ЭВ — вывод кабеля), ×N — число постов в рамке, гр. — группа щита, H — высота оси от чистого пола, мм; группы по клавишам выключателя — на листе выключателей.
4. Схема мебели, приборов и декора не является технической документацией для производства мебели; габариты — по паспортам изделий.
5. Картины и зеркала крепить к основанию по паспорту изделия (закладные и анкеры — в перечне скрытых работ); крест — ось центра предмета.
6. Карнизы (шины) — по ведомости текстиля декоратора; длина L и верх H — по развёртке, крепление — до окраски потолка.
7. Потолок на развёртках — по нижнему уровню У1; другие уровни потолка помещения: У2 +2,600.

1000 мм · печать 1:1

Изм.	Кол.уч	Лист	№ док.	Подп.	Дата
Разраб.		Кырлан А.С.			21.10.26
Пров.					
ГИП					
Н. контр.					
Утв.					

ГД-2026-010-АИ

Дом 331 м²

Общая площадь 270,67* м² · * размеры приняты, не замерены (реестр — л. 7, К-1)

Дизайн-проект интерьера

Стадия	Лист	Листов
РП	145	159

Развёртки стен В, Г. Спальня 4 (пом. 19)

М 1:40

Кырлан Александр Сергеевич

выпуск 18.10.2026 № 9365d64cec · стр. 151 из 197

Развёртка стены А. Санузел 2 (пом. 20)

Санузел 2 (пом. 20) · вид изнутри помещения · размеры в мм, отметки в м

ПРЕДВАРИТЕЛЬНО · не для производства работ · открыто пунктов: 6 (реестр — л. 7)

Развёртка стены А

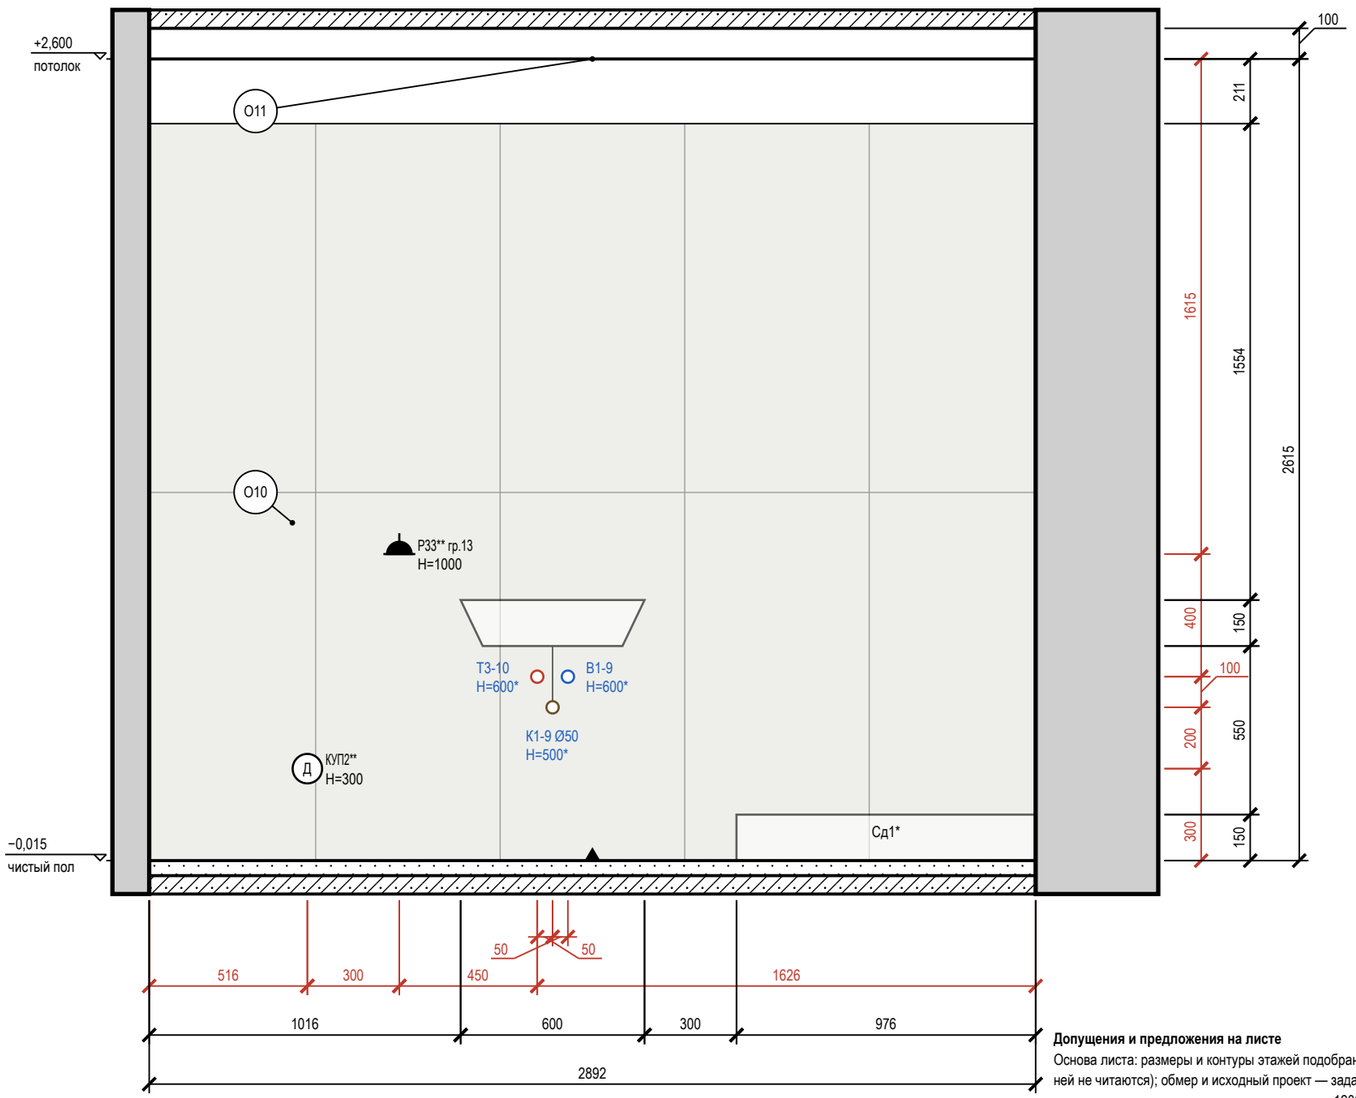

Схема развёрток (М 1:100)

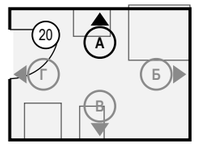

Условные обозначения

- розетка влагозащищённая IP44
- вывод В1 (код — в ведомости привязок)
- вывод Т3 (код — в ведомости привязок)
- вывод К1 (код — в ведомости привязок)
- привязки точек и выводов от угла и от пола, мм
- мебель и приборы — фасад по расстановке (условно)
- стены и перекрытия в сечении
- плитка: сетка швов по формату, ▲ — ось старта
- О1 — марка отделки по реестру отделки альбома
- А — марка развёртки: буква стены, стрелка — взгляд

Ведомость отделки (на листе)

Марка	Поверхность	Материал, изделие	Цвет, код	Кол.
О10	стены	облицовка плиткой, Atlas Concorde Marvel Travertine, 600×1200×9 мм, A8UZ, затирка CG2WA	Atlas Concorde A8UZ «Marvel Travertine»	7 м²
О11	потолок	окраска, Tikkurila Luja 7, матовая, подготовка Q3	Little Greene No. 105 «Slaked Lime»	6,3 м²

Допущения и предложения на листе

Основа листа: размеры и контуры этажей подобраны проектировщиком по составу помещений и площадям этажей с картинки 470 px (размеры на ней не читаются); обмер и исходный проект — задание (К-1); высоты: 1-й этаж 2800 мм, мансарда 2700 мм (горизонтальная часть) приняты; скаты кровли мансарды приняты по картинке: колено 1200 мм, уклон 45°, конёк вдоль длинной стороны; проект КР — задание (К-2); наружные стены 400 мм, перегородки 120 мм приняты (К-1); разрешённая мощность 15 кВт принята по типовым ТУ для частного дома (К-4); подрайон климата не задан — принят не северный (жилые от 2,5 м) (К-7).

Знак «**» — предложение проектировщика, заказчиком не утверждено (согласовать с заказчиком): записи в реестре нет: Р33 — по образцу: Розетка Р33 на высоте 1100 мм, вне шва плитки; КУП2 — по образцу: Добавлены выводы к вентиляторам: ЭВ4 (ВР1, ванная) и ЭВ5 (ВР3, санузел 2) — группа 3, высота 2389 мм, включение с основным светом, таймер выбега в вентиляторе; и коробки уравнивания потенциалов КУП1 (ванная) и КУП2 (санузел 2) — высота 300 мм, у входа, вне зон 0–2, проводник от шины PE щита ЩК, сече.

См. лист открытых вопросов (лист 7, записи К-1, К-2, К-4, К-7).

Примечания

1. Развёртки — вид на стену изнутри помещения, по часовой стрелке; расположение — на схеме листа и на листе 102; размеры — в мм по чистовым поверхностям; отметки — в м от ±0,000; высоты Н — от чистого пола помещения до оси изделия, у декора — до центра.
2. Красные цепочки — привязки электроточек и выводов: по горизонтали от угла чистовых стен, по вертикали от чистого пола, до оси изделия; звенья короче 3 мм на листе вынесены во второй ярус (ближняя к стене цепочка).
3. У знака электроточки: марка (Р — розетка, S — выключатель, Св — светильник, ЭВ — вывод кабеля), ×N — число постов в рамке, гр. — группа щита, Н — высота оси от чистого пола, мм; группы по клавишам выключателя — на листе выключателей.
4. Схема мебели, приборов и декора не является технической документацией для производства мебели; габариты — по паспортам изделий (* — высота не задана в проекте, показана по типовому изделию).
5. Выводы ВК — коды и высоты по листу выводов сантехники; * — высота принята по типовой практике монтажа, окончательно — по паспорту прибора.
6. Облицовка — по сетке швов 2 мм, раскладка от оси стены (треугольник у пола), целые ряды от пола; подрезки — по листу раскладки плитки.
7. Гидроизоляция в 2 слоя, заход на стены 200 мм — до облицовки, с актом скрытых работ и тестом проливом (узел — на листе узлов).

1000 мм · печать 1:1

Изм.	Кол.уч	Лист	№ док.	Подп.	Дата
Разраб.		Кырлан А.С.			21.10.26
Пров.					
ГИП					
Н. контр.					
Утв.					

ГД-2026-010-АИ

Дом 331 м²

Общая площадь 270,67* м² · * размеры приняты, не замерены (реестр — л. 7, К-1)

Дизайн-проект интерьера

Стадия	Лист	Листов
РП	146	159

Развёртка стены А. Санузел 2 (пом. 20)

М 1:20

Кырлан Александр Сергеевич

выпуск 18.10.2026 № 9365d64cec · стр. 152 из 197

Развёртки стен Б, В. Санузел 2 (пом. 20)

Санузел 2 (пом. 20) · вид изнутри помещения · размеры в мм, отметки в м

ПРЕДВАРИТЕЛЬНО · не для производства работ · открыто пунктов: 6 (реестр — л. 7)

Развёртка стены Б

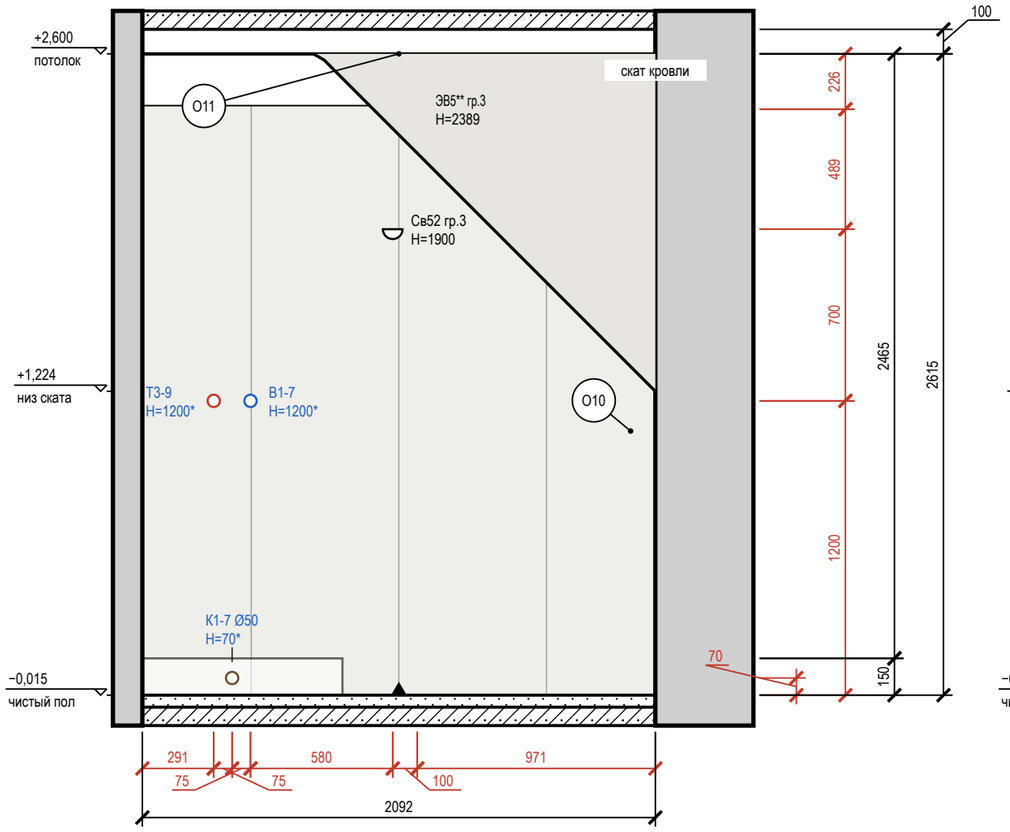

Развёртка стены В

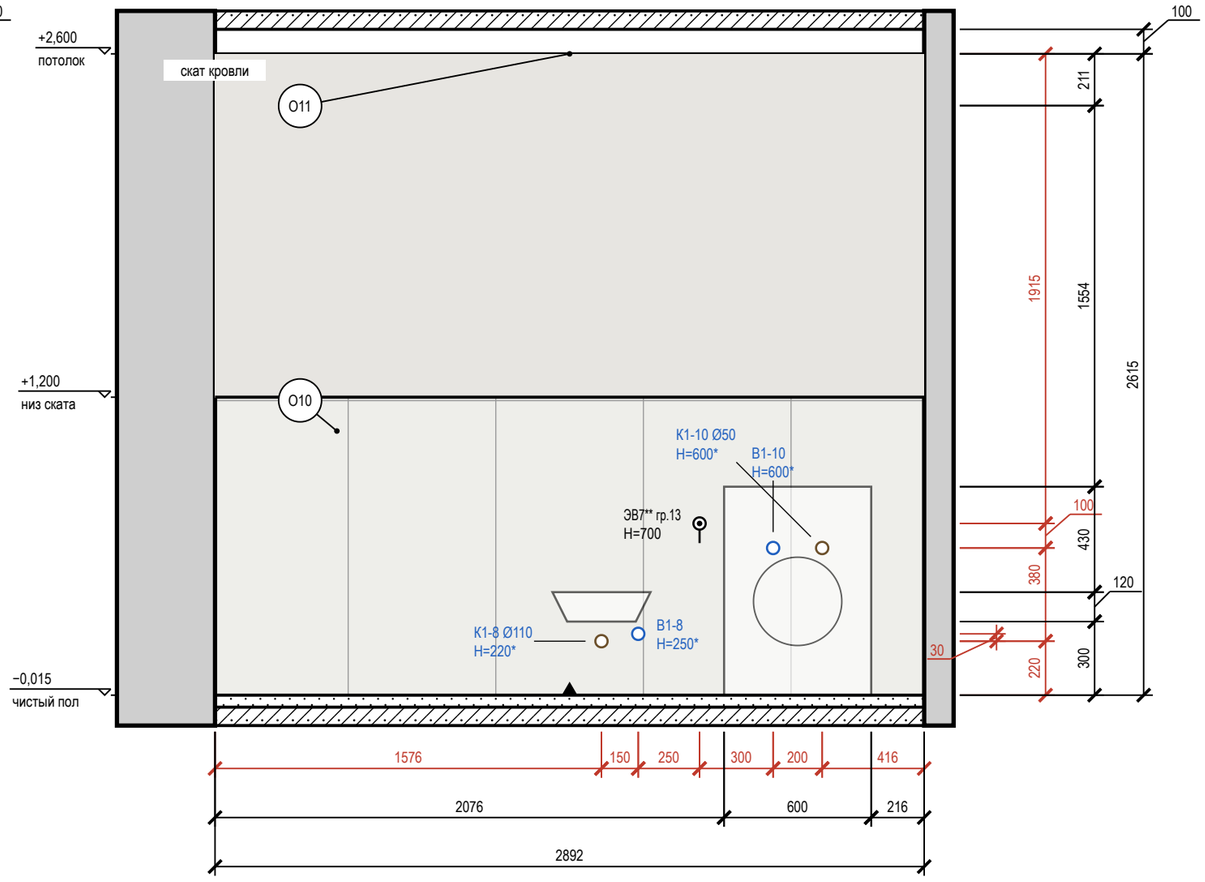

Схема развёрток (М 1:100)

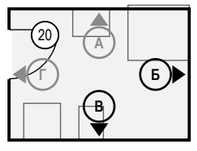

Условные обозначения

- вывод кабеля для подключения прибора (без розетки), марка ЭВ
- светильник настенный (бра), H — высота оси
- вывод В1 (код — в ведомости привязок)
- вывод Т3 (код — в ведомости привязок)
- вывод К1 (код — в ведомости привязок)
- привязки точек и выводов от угла и от пола, мм
- мебель и приборы — фасад по расстановке (условно)
- стены и перекрытия в сечении
- плитка: сетка швов по формату, ▲ — ось старта
- О1 — марка отделки по реестру отделки альбома
- А — марка развёртки: буква стены, стрелка — взгляд

Ведомость отделки (на листе)

Марка	Поверхность	Материал, изделие	Цвет, код	Кол.
О10	стены	облицовка плиткой, Atlas Concorde Marvel Travertine, 600×1200×9 мм, A8UZ, затирка CG2WA	Atlas Concorde A8UZ «Marvel Travertine»	12 м²
О11	потолок	окраска, Tikkurila Luja 7, матовая, подготовка Q3	Little Greene No. 105 «Slaked Lime»	6,3 м²

Примечания

1. Развёртки — вид на стену изнутри помещения, по часовой стрелке; расположение — на схеме листа и на листе 102; размеры — в мм по чистовым поверхностям; отметки — в м от ±0,000; высоты H — от чистого пола помещения до оси изделия, у декора — до центра.
2. Красные цепочки — привязки электроточек и выводов: по горизонтали от угла чистовых стен, по вертикали от чистого пола, до оси изделия; звенья короче 3 мм на листе вынесены во второй ярус (ближняя к стене цепочка).
3. У знака электроточки: марка (Р — розетка, S — выключатель, Св — светильник, ЭВ — вывод кабеля), ×N — число постов в рамке, гр. — группа щита, H — высота оси от чистого пола, мм; группы по клавишам выключателя — на листе выключателей.
4. Схема мебели, приборов и декора не является технической документацией для производства мебели; габариты — по паспортам изделий (* — высота не задана в проекте, показана по типовому изделию).
5. Выводы ВК — коды и высоты по листу выводов сантехники; * — высота принята по типовой практике монтажа, окончательно — по паспорту прибора.
6. Облицовка — по сетке швов 2 мм, раскладка от оси стены (треугольник у пола), целые ряды от пола; подрезки — по листу раскладки плитки.
7. Гидроизоляция в 2 слоя, заход на стены 200 мм — до облицовки, с актом скрытых работ и тестом проливом (узел — на листе узлов).

1000 мм · печать 1:1

Допущения и предложения на листе. Знак «**» предложено (согласовать). См. лист открытых вопросов (лист 7).

Изм.	Кол.уч	Лист	№ док.	Подп.	Дата
Разраб.		Кырлан А.С.			21.10.26
Пров.					
ГИП					
Н. контр.					
Утв.					

ГД-2026-010-АИ

Дом 331 м²

Общая площадь 270,67* м² · * размеры приняты, не замерены (реестр — л. 7, К-1)

Дизайн-проект интерьера

Стадия	Лист	Листов
РП	147	159

Развёртки стен Б, В. Санузел 2 (пом. 20)

М 1:25

Кырлан Александр Сергеевич

выпуск 18.10.2026 № 9365d64cec · стр. 153 из 197

Развёртка стены Г. Санузел 2 (пом. 20)

Санузел 2 (пом. 20) · вид изнутри помещения · размеры в мм, отметки в м

ПРЕДВАРИТЕЛЬНО · не для производства работ · открыто пунктов: 6 (реестр — л. 7)

Развёртка стены Г

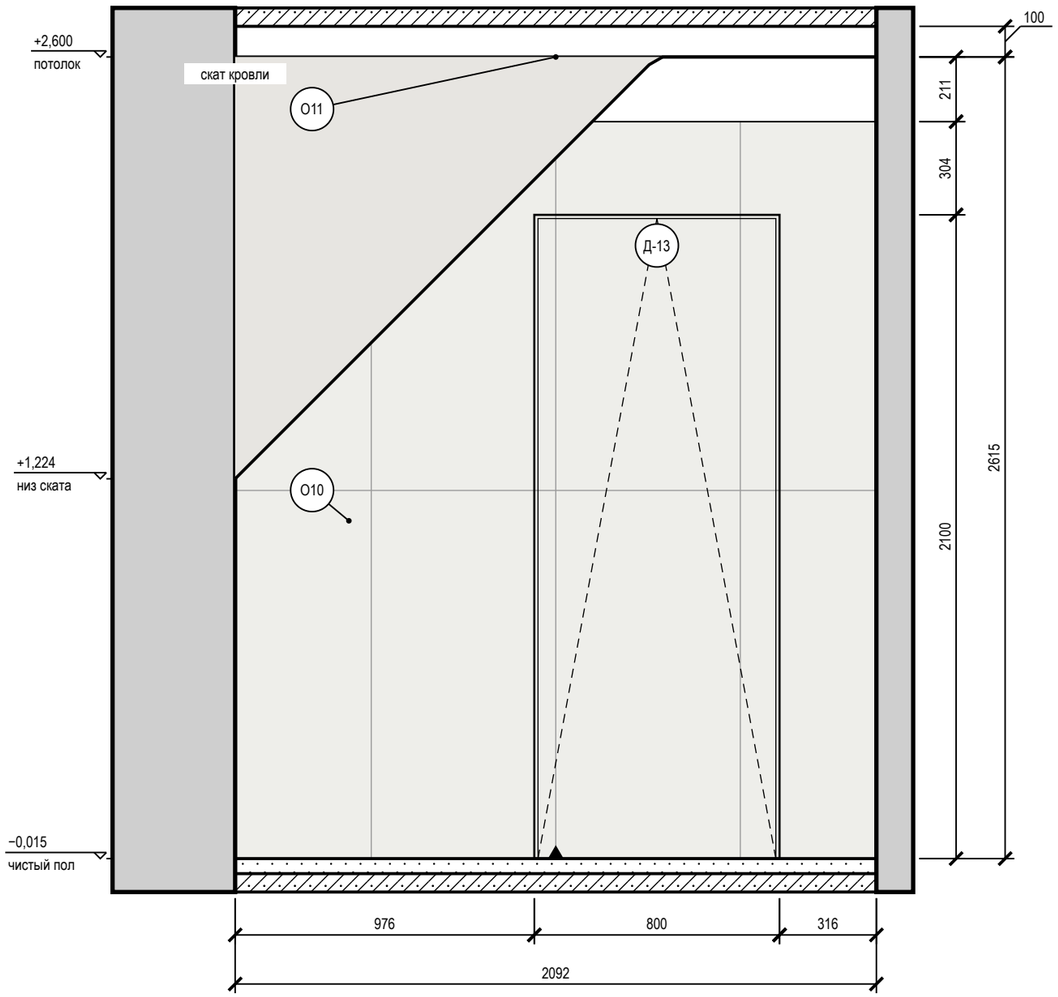

Схема развёрток (М 1:100)

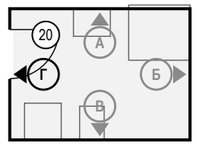

Условные обозначения

- привязки точек и выводов от угла и от пола, мм
- мебель и приборы — фасад по расстановке (условно)
- дверь скрытого монтажа: полотно в плоскости стены (узел — на листе узлов)
- стены и перекрытия в сечении
- плитка: сетка швов по формату, ▲ — ось старта
- О1 — марка отделки по реестру отделки альбома
- А — марка развёртки: буква стены, стрелка — взгляд

Ведомость отделки (на листе)

Марка	Поверхность	Материал, изделие	Цвет, код	Кол.
О10	стены	облицовка плиткой, Atlas Concorde Marvel Travertine, 600×1200×9 мм, A8UZ, затирка CG2WA	Atlas Concorde A8UZ «Marvel Travertine»	3,3 м²
О11	потолок	окраска, Tikkurila Luja 7, матовая, подготовка Q3	Little Greene No. 105 «Slaked Lime»	6,3 м²

Допущения и предложения на листе

Основа листа: размеры и контуры этажей подобраны проектировщиком по составу помещений и площадям этажей с картинки 470 px (размеры на ней не читаются); обмер и исходный проект — задание (К-1); высоты: 1-й этаж 2800 мм, мансарда 2700 мм (горизонтальная часть) приняты; скаты кровли мансарды приняты по картинке: колено 1200 мм, уклон 45°, конёк вдоль длинной стороны; проект КР — задание (К-2); наружные стены 400 мм, перегородки 120 мм приняты (К-1); разрешённая мощность 15 кВт принята по типовым ТУ для частного дома (К-4); подрайон климата не задан — принят не северный (жилые от 2,5 м) (К-7).

См. лист открытых вопросов (лист 7, записи К-1, К-2, К-4, К-7).

Примечания

1. Развёртки — вид на стену изнутри помещения, по часовой стрелке; расположение — на схеме листа и на листе 102; размеры — в мм по чистовым поверхностям; отметки — в м от ±0,000; высоты Н — от чистого пола помещения до оси изделия, у декора — до центра.
2. Красные цепочки — привязки электроточек и выводов: по горизонтали от угла чистовых стен, по вертикали от чистого пола, до оси изделия; звенья короче 3 мм на листе вынесены во второй ярус (ближняя к стене цепочка).
3. У знака электроточки: марка (Р — розетка, S — выключатель, Св — светильник, ЭВ — вывод кабеля), ×N — число постов в рамке, гр. — группа щита, Н — высота оси от чистого пола, мм; группы по клавишам выключателя — на листе выключателей.
4. Схема мебели, приборов и декора не является технической документацией для производства мебели; габариты — по паспортам изделий.
5. Облицовка — по сетке швов 2 мм, раскладка от оси стены (треугольник у пола), целые ряды от пола; подрезки — по листу раскладки плитки.
6. Гидроизоляция в 2 слоя, заход на стены 200 мм — до облицовки, с актом скрытых работ и тестом проливом (узел — на листе узлов).
7. Двери скрытого монтажа — полотно в плоскости стены, отделка стены по полотну, плинтус прерывается у короба (узел — на листе узлов).

1000 мм · печать 1:1

Изм.	Кол.уч	Лист	№ док.	Подп.	Дата
Разраб.		Кырлан А.С.			21.10.26
Пров.					
ГИП					
Н. контр.					
Утв.					

ГД-2026-010-АИ

Дом 331 м²

Общая площадь 270,67* м² · * размеры приняты, не замерены (реестр — л. 7, К-1)

Дизайн-проект интерьера

Стадия	Лист	Листов
РП	148	159

Развёртка стены Г. Санузел 2 (пом. 20)

М 1:20

Кырлан Александр Сергеевич

выпуск 18.10.2026 № 9365d64cec · стр. 154 из 197

Узлы

Пороги и стыки покрытий, скрытые двери, короба стояков, гидроизоляция, плинтус

1 Порог 15 мм: мокрая зона — жилое помещение (М 1:10)

Применение: двери Д-2, Д-9, Д-13; места — лист 102

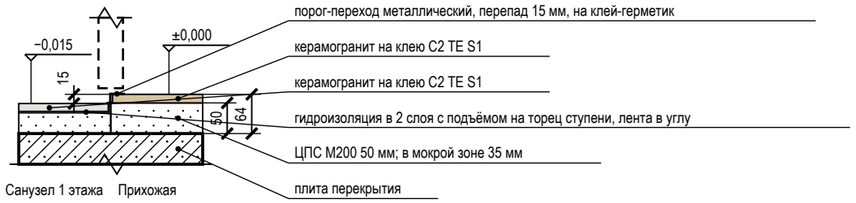

2 Стык покрытий пола Т-профилем без перепада (М 1:5)

Применение: проёмы 5↔11; места — лист 102

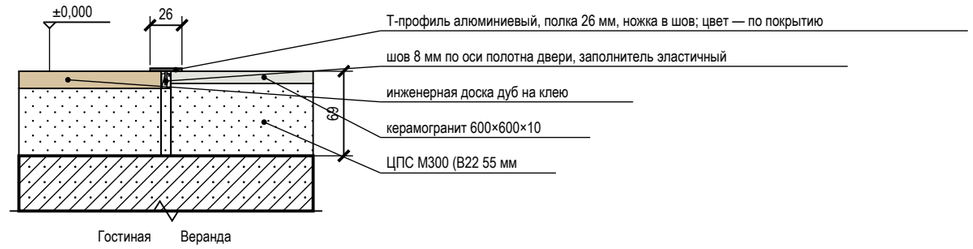

3 Дверь скрытого монтажа в плоскости стены, плинтус (М 1:5)

Применение: двери Д-1, Д-2, Д-7, Д-8, Д-9, Д-10, Д-11, Д-12, Д-13; места — лист 102

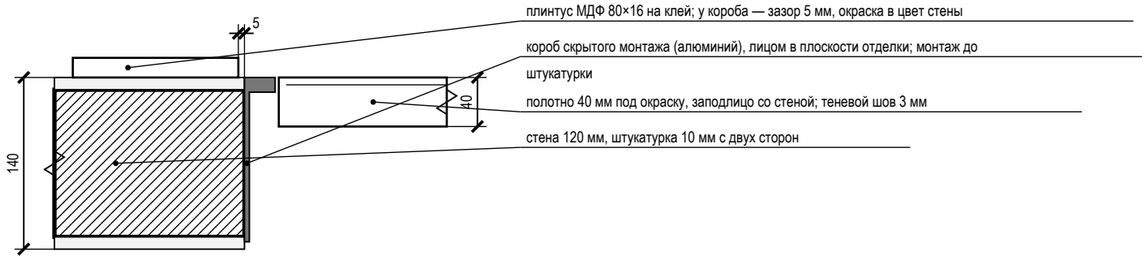

4 Короб стояков К1-1 с люком и звукоизоляцией (М 1:20)

Применение: пом. 3, 1, 8; места — лист 102

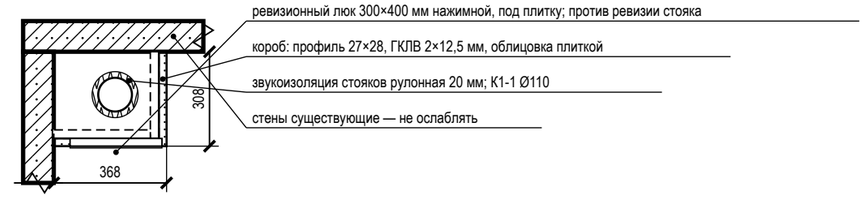

5 Гидроизоляция санузла: заход на стены 200 мм, примыкание ванны (М 1:20)

Применение: пом. 3, 15, 20; места — лист 102

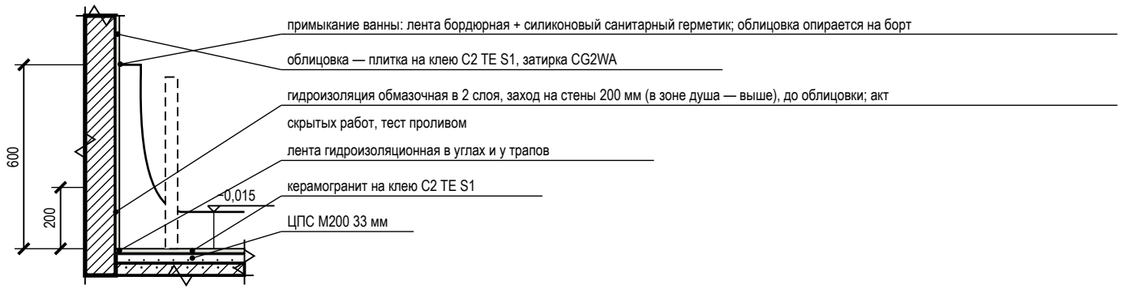

6 Плинтус МДФ 80×16 мм у окрашенной стены (М 1:10)

Применение: пом. 1, 2, 4, 5, 6, 7, 8, 9, 10, 13, 14, 16, 17, 18, 19; места — лист 102

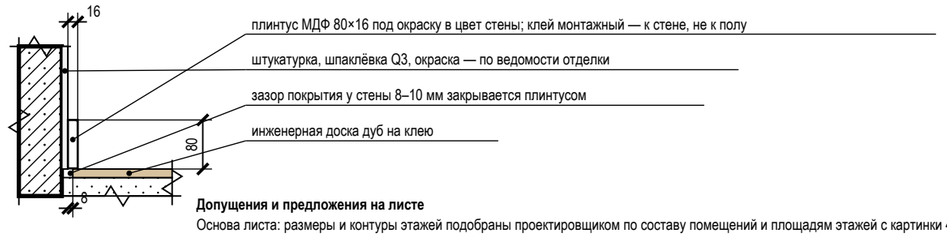

Допущения и предложения на листе

Основа листа: размеры и контуры этажей подобраны проектировщиком по составу помещений и площадям этажей с картинки 470 px (размеры на ней не читаются); обмер и исходный проект — задание (К-1); высоты: 1-й этаж 2800 мм, мансарда 2700 мм (горизонтальная часть) приняты; скаты кровли мансарды приняты по картинке: колено 1200 мм, уклон 45°, конёк вдоль длинной стороны; проект КР — задание (К-2); наружные стены 400 мм, перегородки 120 мм приняты (К-1); разрешённая мощность 15 кВт принята по типовым ТУ для частного дома (К-4); подрайон климата не задан — принят не северный (жилые от 2,5 м) (К-7).

См. лист открытых вопросов (лист 7, записи К-1, К-2, К-4, К-7).

Условные обозначения

- железобетон (плита, стены)
- кладка, перегородка
- стяжка, раствор
- гипсокартон ГКЛВ
- звукоизоляция, эластичный заполнитель
- плитка, керамогранит на клею
- инженерная доска (покрытие пола)
- металлический профиль (порог, Т-профиль, короб двери)
- гидроизоляция (обмазочная, лента)

Примечания

1. Узлы — типовые решения проекта для мест, отмеченных выносками на листе схемы расположения развёрток и узлов; размеры — в мм, отметки — в м от ±0,000.
2. Узлы с гидроизоляцией, закладными и коробами скрытого монтажа принимаются по актам скрытых работ до закрытия отделкой; гидроизоляция — после теста проливом (24 ч).
3. Марки изделий (порог, Т-профиль, короб скрытой двери, люк) — по спецификациям; замена — на аналог с теми же габаритами по согласованию с автором проекта.

Изм.	Кол.уч	Лист	№ док.	Подп.	Дата
Разраб.		Кырлан А.С.			21.10.26
Пров.					
ГИП					
Н. контр.					
Утв.					

ГД-2026-010-АИ

Дом 331 м²

Общая площадь 270,67* м² · * размеры приняты, не замерены (реестр — л. 7, К-1)

Дизайн-проект интерьера

Стадия	Лист	Листов
РП	149	159

Узлы

М б/м

Кырлан Александр Сергеевич

выпуск 18.10.2026 № 9365d64cec · стр. 155 из 197

05

Смета

Кырлан Александр Сергеевич

выпуск 18.10.2026 · 9365d64cec · стр. 156 из 197

Ведомость объёмов работ

ПРЕДВАРИТЕЛЬНО · не для производства работ · открыто пунктов: 6 (реестр — л. 7)

Объёмы по помещениям от чертежа · площади в м², длины в м · формула, правило проёмов и источник в каждой строке

Ведомость объёмов работ по помещениям

Поз.	Наименование работ (материал, число слоёв)	Ед. изм.	Объём по помещениям (№ по экспликации)																				Всего	Формула подсчёта	Правило проёмов	Источник	Цена за ед., ₽	Стоимость, ₽
			1	2	3	4	5	6	7	8	9	10	11	12	13	14	15	16	17	18	19	20						
1. Демонтаж и черновые работы																												
1	Демонтаж существующего покрытия пола до основания	м²	24,59	11,92	4,87	6,88	33,74	10,02	5,99	12,46	3,49	41,58	21,84	3,38	24,59	6,74	6,88	15,52	21,72	17,11	16,28	6,29	295,89	S пом.		л. 15–18	по КП	
2	Демонтаж существующей отделки стен до основания	м²	45,94	30,98	22,48	26,96	45,12	22,29	23,28	38,99	17,07	62,59	49,63	18,73	43,05	25,25	25,50	35,43	40,74	37,80	37,52	24,89	674,24	P × H − проёмы	за вычетом проёмов	л. 15–18	по КП	
3	Демонтаж существующей отделки потолка до основания	м²	24,59	11,92	4,87	6,88	33,74	10,02	5,99	12,46	3,49	41,58	21,84	3,38	24,59	6,74	6,88	15,52	21,72	17,11	16,28	6,29	295,89	S пом.		л. 15–18	по КП	
4	Демонтаж существующих дверных блоков	шт		1	1	1	1		1	1	2	1			1	1	1	1		1	1	1	16	по ведомости проёмов		л. 17–20	по КП	
5	Демонтаж существующих сантехприборов и электрооборудования (если есть)	компл																						по факту на объекте		л. 17, 18	по КП	
6	Устройство стяжки: стяжка ЦПС М300 (В22,5), фибра, по звукоизоляции, 53 мм	м²	24,70	12,06	4,92	7,06	34,04	10,36	6,12	12,68	3,60	42,23			24,68	6,82	6,92	15,62	22,10	17,23	16,33	6,34	273,81	S пом. + S в дверных проёмах (b × t/2)	проёмы добавлены	л. 67, 68, 70–72	530	145 119
7	Гидроизоляция обмазочная, 2 слоя: пол, стены на 200 мм, зоны замачивания	м²			12,14												14,15					12,91	39,20	пол + (P − двери) × h заведения + зоны замачивания		л. 61	450	17 640
8	Штукатурка стен по маякам, до 10 мм	м²	45,94	30,98	22,48	26,96	45,12	22,29	23,28	38,99	17,07	62,59	49,63	18,73	43,05	25,25	25,50	35,43	40,74	37,80	37,52	24,89	674,24	P × H − проёмы по обводу коробок − грани перегородок на ГКЛВ	за вычетом проёмов	л. 15, 16, 70–72	530	357 347
9	Штукатурка оконных откосов шириной более 200 мм	м²	2,97	1,45		0,86	3,04					0,99	5,25		2,90		0,79	1,45		1,45	2,90		24,05	Σ (2h + b) × глубина откоса	откосы > 200 мм	л. 15, 16	540	12 987
10	Потолок ГКЛ по каркасу П113, 1 слой	м²	24,59	11,92	4,87		33,74	6,92		12,46					24,59		6,88	15,52	21,72	17,11	16,28	6,29	202,89	S пом. по плану потолков		л. 55–60	1 500	304 335
11	Балки декоративные 150×120 мм под потолком (фальш-балка, массив лиственницы под маслом): изделие и монтаж на закладные	м					20,76	3,76							7,32				14,40				46,24	4 шт. по плану потолков		л. 55–60	по КП	
Итого по разделу 1 — 837 428 ₽ (позиций 11, из них по КП 6); в сводную смету — л. 158, 159																												
2. Инженерные системы																												
12	Прокладка кабеля ВВГнг(А)-LS по группам щита: за потолком и в штробах стен (штробы — только после технического заключения, см. строку «Штробы в стенах»)	м																					663,00	Σ длин групп щита		л. 39, 40	60	39 780
13	Прокладка слаботочной линии: Кабель домофона — тип по системе поставщика, отдельно от силовых	м																					2,80	по лучам от ЩС**: 1 точ., запас 10 %		л. 43, 44	по КП	
14	Прокладка слаботочной линии: Кабель коаксиальный RG-6 (75 Ом) к розеткам ТВ, отдельно от силовых	м																					70,60	по лучам от ЩС**: 5 точ., запас 10 %		л. 43, 44	по КП	

Допущения и предложения на листе

Основа листа: размеры и контуры этажей подобраны проектировщиком по составу помещений и площадям этажей с картинки 470 px (размеры на ней не читаются); обмер и исходный проект — задание (К-1); высоты: 1-й этаж 2800 мм, мансарда 2700 мм (горизонтальная часть) приняты; скаты кровли мансарды приняты по картинке: колено 1200 мм, уклон 45°, конёк вдоль длинной стороны; проект КР — задание (К-2); наружные стены 400 мм, перегородки 120 мм приняты (К-1); разрешённая мощность 15 кВт принята по типовым ТУ для частного дома (К-4); подрайон климата не задан — принят не северный (жилые от 2,5 м) (К-7).

Знак «**» — предложение проектировщика, заказчиком не утверждено (согласовать с заказчиком): записи в реестре нет: ЩС — щит слаботочный: место и состав.

См. лист открытых вопросов (лист 7, записи К-1, К-2, К-4, К-7).

Изм.	Кол.уч	Лист	№ док.	Подп.	Дата
Разраб.		Кырлан А.С.			21.10.26
Пров.					
ГИП					
Н. контр.					
Утв.					

ГД-2026-010-АИ

Дом 331 м²

Общая площадь 270,67* м² · * размеры приняты, не замерены (реестр — л. 7, К-1)

Дизайн-проект интерьера

Стадия	Лист	Листов
РП	150	159

Ведомость объёмов работ

М б/м

Кырлан Александр Сергеевич

Ведомость объёмов работ (продолжение)

Объёмы по помещениям от чертежа · площади в м², длины в м · формула, правило проёмов и источник в каждой строке

Ведомость объёмов работ по помещениям (продолжение)

Поз.	Наименование работ (материал, число слоёв)	Ед. изм.	Объём по помещениям (№ по экспликации)																				Всего	Формула подсчёта	Правило проёмов	Источник	Цена за ед., ₽	Стоимость, ₽
			1	2	3	4	5	6	7	8	9	10	11	12	13	14	15	16	17	18	19	20						
15	Прокладка слаботочной линии: Кабель U/UTP кат. 5e (LAN, Wi-Fi и камеры по PoE), отдельно от силовых	м																					11,90	по лучам от ЩС**: 1 точ., запас 10 %		л. 43, 44	по КП	
16	Прокладка слаботочной линии: Кабель U/UTP кат. 6 (LAN, Wi-Fi и камеры по PoE), отдельно от силовых	м																					96,40	по лучам от ЩС**: 7 точ., запас 10 %		л. 43, 44	по КП	
17	Прокладка гофротрубы Ø20 для слаботочных линий, отдельно от силовых	м																					163,50	по длине лучей без участков в канале плинтуса (≈ 90 %)		л. 43, 44	по КП	
18	Сборка слаботочного щита ЩС**: корпус, патч-панель, подключение линий и питания 220 В; коммутатор и точки доступа — оборудование заказчика	шт																					1	один щит		л. 37, 38, 43, 44	по КП	
19	Электроточка: подрозетник в бетоне, розетка, выключатель, вывод	шт	17	11	4	2	10	4		8	1	5	1	1	10		4	11	4	11	11	3	118	по ведомости электроточек		л. 31, 32, 37, 38	950	112 100
20	Штробы в стенах под спуски кабеля к точкам — выполняются только после технического заключения о несущих стенах	м	26,35	21,80	5,37	3,50	19,20	7,80		12,40	1,90	7,60	2,53	2,53	18,00		5,37	19,60	7,40	19,60	19,60	3,76	204,31	Σ (H − h) по точкам на стенах: вертикальные спуски	после техзаключения	л. 17, 18, 31, 32	по КП	
21	Установка встраиваемого точечного светильника	шт	7	6	3		8	2		4			1	1	8		3	6	2	6	6	2	65	по плану освещения		л. 33, 34	750	48 750
22	Монтаж светильника: потолочного, подвесного, настенного	шт		2	1	1	1		1		1	2			2	1	1	2		2	2	1	20	по плану освещения		л. 33, 34	1 200	24 000
23	Монтаж LED-ленты в алюминиевый профиль	м	11,40	5,40			21,10			1,80					6,00			3,20		15,50	6,00		70,40	Σ длин лент по плану освещения		л. 33, 34	230	16 192
24	Установка блока питания LED в доступном месте (люк, шкаф)	шт	2	1			1			1					1			1		1	1		9	один на LED-группу		л. 33, 34	570	5 130
25	Установка автономного пожарного извещателя	шт	1	1			1	1		1					1			1	1	1	1		10	по плану розеток		л. 31, 32	по КП	
26	Сборка щита: установка автоматов и АВДТ групп, вводного автомата	шт																					22	группы + вводной автомат		л. 39, 40	230	5 060
27	Установка вводного УЗО	шт																					1	по однолинейной схеме		л. 39, 40	380	380
28	Монтаж инсталляции, установка подвесного унитаза и кнопки смыва	шт			1												1					1	3	по плану выводов		л. 49, 50, 53	10 500	31 500
29	Короб инсталляции: каркас и обшивка ГКЛВ в 2 слоя, ревизионный доступ к смыву	шт			1												1					1	3	по плану выводов		л. 49, 50, 61–66	по КП	
30	Короб К1 над чистым полом: каркас и обшивка ГКЛВ под плитку (материалы в спецификации ВК)	м.п.	1,28		0,54												2,88					5,83	10,53	Σ открытых участков выпусков К1 (профиль листа разводки ВК)		л. 49, 50, 53	по КП	
31	Установка ванны с сифоном	шт															1						1	по плану выводов		л. 49, 50, 53	6 000	6 000

Допущения и предложения на листе

Основа листа: размеры и контуры этажей подобраны проектировщиком по составу помещений и площадям этажей с картинки 470 px (размеры на ней не читаются); обмер и исходный проект — задание (К-1); высоты: 1-й этаж 2800 мм, мансарда 2700 мм (горизонтальная часть) приняты; скаты кровли мансарды приняты по картинке: колено 1200 мм, уклон 45°, конёк вдоль длинной стороны; проект КР — задание (К-2); наружные стены 400 мм, перегородки 120 мм приняты (К-1); разрешённая мощность 15 кВт принята по типовым ТУ для частного дома (К-4); подрайон климата не задан — принят не северный (жилые от 2,5 м) (К-7).

Знак «**» — предложение проектировщика, заказчиком не утверждено (согласовать с заказчиком): записи в реестре нет: ЩС — щит слаботочный: место и состав.

См. лист открытых вопросов (лист 7, записи К-1, К-2, К-4, К-7).

Изм.	Кол.уч	Лист	№ док.	Подп.	Дата
Разраб.		Кырлан А.С.			21.10.26
Пров.					
ГИП					
Н. контр.					
Утв.					

ГД-2026-010-АИ

Дом 331 м²

Общая площадь 270,67* м² · * размеры приняты, не замерены (реестр — л. 7, К-1)

Дизайн-проект интерьера

Стадия	Лист	Листов
РП	151	159

Ведомость объёмов работ (продолжение)

М б/м

Кырлан Александр Сергеевич

Ведомость объёмов работ (продолжение)

Объёмы по помещениям от чертежа · площади в м², длины в м · формула, правило проёмов и источник в каждой строке

Ведомость объёмов работ по помещениям (продолжение)

Поз.	Наименование работ (материал, число слоёв)	Ед. изм.	Объём по помещениям (№ по экспликации)																			Всего	Формула подсчёта	Правило проёмов	Источник	Цена за ед., ₽	Стоимость, ₽
			1	2	3	4	5	6	7	8	9	10	11	12	13	14	15	16	17	18	19	20						
32	Установка умывальника (мойки) с сифоном и смесителем	шт			1												1					1	3	по плану выводов		л. 49, 50, 53	3 000	9 000
33	Установка душевого поддона с трапом, ограждения	шт			1																	1	2	по плану выводов		л. 49, 50, 53	по КП	
34	Подключение стиральной (посудомоечной) машины к ВК	шт																				1	1	по плану выводов		л. 49, 50	по КП	
35	Установка радиатора с узлом подключения и терморегулятором	шт	2	1			2								2			1		1	2		11	по плану отопления		л. 47, 48	по КП	
Итого по разделу 2 — 297 892 ₽ (позиций 24, из них по КП 13); в сводную смету — л. 158, 159																											
3. Чистовые работы																											
36	Облицовка стен керамогранитом 600×1200 на клею	м²			19,67												19,01					17,04	55,72	по раскладке: зона облицовки − место за коробом	за вычетом проёмов	л. 61–66	2 500	139 300
37	Облицовка короба инсталляции (ГКЛВ) керамогранитом: лицо, боковины, полка	м²			1,64												1,73					1,47	4,84	по раскладке: лицо, боковины, полка		л. 61–66	2 500	12 100
38	Укладка керамогранита на пол, 600×1200, на клею	м²			4,92	7,06				12,68	3,60		21,98	3,44			6,92					6,34	66,94	S пом. + S в дверных проёмах	проёмы добавлены	л. 61–68	1 800	120 492
39	Затирка швов керамогранита	м²			26,18	6,88				12,46	3,49		21,84	3,38			27,62					24,80	126,65	Σ S облицовки и пола из плитки		л. 61–66	150	18 998
40	Грунтование стен, 2 слоя (под штукатурку и под отделку)	м²	45,94	30,98	22,48	26,96	45,12	22,29	23,28	38,99	17,07	62,59	49,63	18,73	43,05	25,25	25,50	35,43	40,74	37,80	37,52	24,89	674,24	P × H − проёмы	за вычетом проёмов	л. 70–72	96	64 727
41	Шпаклёвка стен под окраску, 2 слоя (старт и финиш), уровень К3	м²	45,94	30,98		26,96	45,12	22,29	23,28	38,99	17,07	62,59	49,63	18,73	43,05	25,25		35,43	40,74	37,80	37,52		601,37	P × H − проёмы − фартук	за вычетом проёмов	л. 70–72	750	451 028
42	Грунтование и шпаклёвка оконных откосов, 2 слоя	м.п.	9,00	4,40		2,60	9,20					3,00	15,90		8,80			4,40		4,40	8,80		70,50	Σ (2h + b) по окнам	по окнам	л. 15, 16	300	21 150
43	Грунтование потолка, 2 слоя	м²	24,59	11,92	4,87	6,88	33,74	10,02	5,99	12,46	3,49	41,58	21,84	3,38	24,59	6,74	6,88	15,52	21,72	17,11	16,28	6,29	295,89	S пом.		л. 70–72	96	28 405
44	Шпаклёвка потолка под окраску, 2 слоя, уровень Q3	м²	24,59	11,92	4,87	6,88	33,74	10,02	5,99	12,46	3,49	41,58	21,84	3,38	24,59	6,74	6,88	15,52	21,72	17,11	16,28	6,29	295,89	S пом.		л. 55–60, 70–72	950	281 096
45	Окраска потолка водно-дисперсионной краской, 2 слоя	м²	24,59	11,92	4,87	6,88	33,74	10,02	5,99	12,46	3,49	41,58	21,84	3,38	24,59	6,74	6,88	15,52	21,72	17,11	16,28	6,29	295,89	S пом.		л. 70–72	360	106 520
46	Окраска стен водно-дисперсионной краской, 2 слоя	м²	54,43	37,91		29,57	60,42	34,34	27,78	46,55	21,06	72,46	64,75	20,83	50,40	28,19		41,10	54,18	44,10	43,40		731,47	P × H − фартук, проёмы не вычитаются	без вычета проёмов	л. 70–72	300	219 441
47	Окраска оконных откосов, 2 слоя	м.п.	9,00	4,40		2,60	9,20					3,00	15,90		8,80			4,40		4,40	8,80		70,50	Σ (2h + b) по окнам	по окнам	л. 15, 16	120	8 460
48	Укладка инженерной доски на клей	м²	24,70	12,06			34,04	10,36	6,12						24,68	6,82		15,62	22,10	17,23	16,33		190,06	S пом. + S в дверных проёмах	проёмы добавлены	л. 67, 68, 70–72	1 200	228 072
49	Установка плинтуса МДФ h=80 мм	м.п.	18,26	11,74		9,66	18,24	6,98	7,78	13,64	5,62				18,66	9,04		14,74	14,44	15,64	16,56		181,00	P − ширина дверных проёмов		л. 70–72	450	81 450
50	Установка плинтуса ПВХ h=100 мм	м.п.										21,98											21,98	P − ширина дверных проёмов		л. 70–72	450	9 891

Допущения и предложения на листе

Основа листа: размеры и контуры этажей подобраны проектировщиком по составу помещений и площадям этажей с картинки 470 px (размеры на ней не читаются); обмер и исходный проект — задание (К-1); высоты: 1-й этаж 2800 мм, мансарда 2700 мм (горизонтальная часть) приняты; скаты кровли мансарды приняты по картинке: колено 1200 мм, уклон 45°, конёк вдоль длинной стороны; проект КР — задание (К-2); наружные стены 400 мм, перегородки 120 мм приняты (К-1); разрешённая мощность 15 кВт принята по типовым ТУ для частного дома (К-4); подрайон климата не задан — принят не северный (жилые от 2,5 м) (К-7).

См. лист открытых вопросов (лист 7, записи К-1, К-2, К-4, К-7).

Изм.	Кол.уч	Лист	№ док.	Подп.	Дата
Разраб.		Кырлан А.С.			21.10.26
Пров.					
ГИП					
Н. контр.					
Утв.					

ГД-2026-010-АИ

Дом 331 м²

Общая площадь 270,67* м² · * размеры приняты, не замерены (реестр — л. 7, К-1)

Дизайн-проект интерьера

Стадия	Лист	Листов
РП	152	159

Ведомость объёмов работ (продолжение)

М б/м

Кырлан Александр Сергеевич

Ведомость объёмов работ (продолжение)

Объёмы по помещениям от чертежа · площади в м², длины в м · формула, правило проёмов и источник в каждой строке

Ведомость объёмов работ по помещениям (продолжение)

Поз.	Наименование работ (материал, число слоёв)	Ед. изм.	Объём по помещениям (№ по экспликации)																				Всего	Формула подсчёта	Правило проёмов	Источник	Цена за ед., ₽	Стоимость, ₽
			1	2	3	4	5	6	7	8	9	10	11	12	13	14	15	16	17	18	19	20						
51	Плинтус из керамогранита: нарезка полос из плитки пола, запил кромки 45°, установка h=80 мм	м.п.											20,48	6,36									26,84	P − ширина дверных проёмов		л. 70–72	930	24 961
52	Окраска плинтуса в тоне S 0804-Y30R, 2 слоя	м.п.	18,26	11,74		9,66	18,24	6,98	7,78	13,64	5,62				18,66	9,04		14,74	14,44	15,64	16,56		181,00	как плинтус		л. 70–72	300	54 300
53	Монтаж дверей скрытого монтажа под покраску (поставщик дверей)	шт		1	1										1	1	1	1		1	1	1	9	по ведомости проёмов		л. 19, 20	5 250	47 250
54	Монтаж межкомнатных дверей (поставщик дверей)	шт					1		1	1	1												4	по ведомости проёмов		л. 19, 20	5 250	21 000
55	Входная дверь, поставка с монтажом и откосами	шт																					3	по ведомости проёмов		л. 19, 20	по КП	
Итого по разделу 3 — 1 938 641 ₽ (позиций 20, из них по КП 1); в сводную смету — л. 158, 159																												

Допущения и предложения на листе

Основа листа: размеры и контуры этажей подобраны проектировщиком по составу помещений и площадям этажей с картинки 470 px (размеры на ней не читаются); обмер и исходный проект — задание (К-1); высоты: 1-й этаж 2800 мм, мансарда 2700 мм (горизонтальная часть) приняты; скаты кровли мансарды приняты по картинке: колено 1200 мм, уклон 45°, конёк вдоль длинной стороны; проект КР — задание (К-2); наружные стены 400 мм, перегородки 120 мм приняты (К-1); разрешённая мощность 15 кВт принята по типовым ТУ для частного дома (К-4); подрайон климата не задан — принят не северный (жилые от 2,5 м) (К-7).

См. лист открытых вопросов (лист 7, записи К-1, К-2, К-4, К-7).

Изм.	Кол.уч	Лист	№ док.	Подп.	Дата
Разраб.		Кырлан А.С.			21.10.26
Пров.					
ГИП					
Н. контр.					
Утв.					

ГД-2026-010-АИ

Дом 331 м²

Общая площадь 270,67* м² · * размеры приняты, не замерены (реестр — л. 7, К-1)

Дизайн-проект интерьера

Стадия	Лист	Листов
РП	153	159

Ведомость объёмов работ (продолжение)

М б/м

Кырлан Александр Сергеевич

Ведомость объёмов работ (окончание)

Объёмы по помещениям от чертежа · площади в м², длины в м · формула, правило проёмов и источник в каждой строке

ПРЕДВАРИТЕЛЬНО · не для производства работ · открыто пунктов: 6 (реестр — л. 7)

Ведомость подсчёта площадей по помещениям

№	Помещение	S пола, м²	P, м	H, м	P × H, м²	Проёмы, м²	Стены нетто, м²	В дверных проёмах, м²	Плинтус, м	Откосы, м.п.
1	Кухня-столовая	24,59	20,16	2,70	54,43	8,49	45,94	0,11	18,26	9,00
2	Кабинет-гостевая	11,92	14,04	2,70	37,91	6,93	30,98	0,14	11,74	4,40
3	Санузел 1 этажа	4,87	9,24	2,62	24,16	1,68	22,48	0,05	нет	нет
4	Котельная	6,88	10,56	2,80	29,57	2,61	26,96	0,18	9,66	2,60
5	Гостиная	33,74	23,24	2,60	60,42	15,30	45,12	0,30	18,24	9,20
6	Холл с лестницей	10,02	12,72	2,70	34,34	12,05	22,29	0,34	6,98	нет
7	Кладовая	5,99	9,92	2,80	27,78	4,49	23,28	0,13	7,78	нет
8	Прихожая	12,46	17,24	2,70	46,55	7,56	38,99	0,22	13,64	нет
9	Тамбур	3,49	7,52	2,80	21,06	3,99	17,07	0,11	5,62	нет
10	Гараж	41,58	25,88	2,80	72,46	9,87	62,59	0,65	21,98	3,00
11	Веранда	21,84	22,88	2,83	64,75	15,12	49,63	0,14	20,48	15,90
12	Крыльцо	3,38	7,36	2,83	20,83	2,10	18,73	0,06	6,36	нет
13	Спальня мастер	24,59	20,16	2,50	50,40	7,35	43,05	0,09	18,66	8,80
14	Гардеробная мастер	6,74	10,44	2,70	28,19	2,94	25,25	0,08	9,04	нет
15	Санузел мастер	6,88	10,56	2,62	27,61	2,11	25,50	0,04	нет	2,40
16	Спальня 2	15,52	16,44	2,50	41,10	5,67	35,43	0,10	14,74	4,40
17	Холл мансарды	21,72	20,84	2,60	54,18	13,44	40,74	0,38	14,44	нет
18	Спальня 3	17,11	17,64	2,50	44,10	6,30	37,80	0,12	15,64	4,40
19	Спальня 4	16,28	17,36	2,50	43,40	5,88	37,52	0,05	16,56	8,80
20	Санузел 2	6,29	10,16	2,62	26,57	1,68	24,89	0,05	нет	нет
	Итого	**295,89**			**809,82**	**135,57**	**674,25**	**3,36**	**229,82**	**72,90**

Реестр контрольных сумм

Показатель	По ВОР	По чертежу	Расхождение	Лист
Σ площадей помещений без летних, м² — общая площадь по экспликации	270,67	270,67	0,0 %	л. 15, 16
Стены под окраску, м² (шпаклёвка) ведомость отделки	601,37	575,14	4,6 %	л. 70–72
Потолки под окраску, м² — ведомость отделки	295,89	295,89	0,0 %	л. 70–72
Плинтус, м — ведомость отделки	229,82	229,82	0,0 %	л. 70–72
Плитка к заказу, шт — ведомость плитки	282	282	0,0 %	л. 61
Гидроизоляция, м² — ведомость материалов плитки	39,20	39,20	0,0 %	л. 61
Точки ЭОМ, шт — планы ЭОМ (без щитов)	232	235	-1,3 %	л. 31–34

Примечания

1. Объёмы — от геометрии проекта (та же, что на планах и в ведомости отделки), не от общей площади: P — периметр чистого контура, H — от чистого пола до низа потолка, проёмы — по наружному обводу коробок.
2. Подсчёт по ГЭСН-2001-15 и ГЭСН-2001-11: штукатурка и шпаклёвка стен — за вычетом проёмов; окраска водными составами — без вычета проёмов (п. 2.24); откосы — отдельно, по ширине до 200 и более 200 мм; полы — с площадью в дверных проёмах.
3. Плитка — по раскладке (целые и с подрезкой); короб инсталляции и фартук — отдельными строками, двойного счёта облицовки нет. Материалы, запас и количество к заказу — в спецификации материалов.
4. Цены — ориентир по открытым прайсам Москвы (прайсы собраны 21.09.2026, часть расценок сверена повторно 24.09.2026), не коммерческое предложение; «по КП» — расценки нет, строка в итог не входит.
5. Демонтаж — по плану демонтажа и общим указаниям: покрытия пола, отделка стен и потолков, дверные блоки — до основания; объёмы справочные, уточняются по факту на объекте (расценки в книге нет — «по КП»).
6. Штробы в стенах — только после технического заключения о несущих стенах (общие указания, план обмера и демонтажа): строка «Штробы в стенах» вертикальные спуски кабеля от потолочной трассы к точкам, объём не меньше фактического (горизонтальные трассы — по исполнительной схеме). Расценки штробления в прайсе нет — «по КП», в итог не входит; кабель в штробах стен прокладывается после неё.
7. Площадь облицовки стен — одно число с тремя названиями: зона облицовки по ведомости отделки 58,23 м² − место за коробом инсталляции 2,51 м² (плитку туда не кладут) = стены под плитку 55,72 м² (строка «Облицовка стен»); облицовка коробов 4,84 м² — отдельной строкой; стены и короба вместе — 60,56 м² (столько плитки по раскладке в спецификации). Источник — один (quantities.js), расхождение на листах ловит.
8. Слаботочные сети: кабель по лучам от ЩС** 181,70 м (U/UTP, RG-6, домофон — по видам), гофра 163,50 м, щит ЩС** с патч-панелью; розетки RJ45 и ТВ монтируются в строке «Электроточка». Длины те же, что в ведомости изделий электрика (одна модель — lowcurrent-engineer/bom.js); оборудование заказчика (точки доступа, камеры, коммутатор) в спецификацию не входит. 2 точ. — предложение листа слаботочки.
9. Коробы: стояков (нет) и К1 над чистым полом (10,53 м открытых участков; труба К1 вдоль стен 31,23 м в короб не зашивается — она за приборами, в раме инсталляции и в шахтах). В спецификации ВК короб К1 заказывается с запасом 10 % — 11,60 м. Материалы коробов стояков и инсталляции — в спецификации материалов, К1 — в спецификации ВК.

Допущения и предложения на листе

Основа листа: размеры и контуры этажей подобраны проектировщиком по составу помещений и площадям этажей с картинки 470 px (размеры на ней не читаются); обмер и исходный проект — задание (К-1); высоты: 1-й этаж 2800 мм, мансарда 2700 мм (горизонтальная часть) приняты; скаты кровли мансарды приняты по картинке: колено 1200 мм, уклон 45°, конёк вдоль длинной стороны; проект КР — задание (К-2); наружные стены 400 мм, перегородки 120 мм приняты (К-1); разрешённая мощность 15 кВт принята по типовым ТУ для частного дома (К-4); подрайон климата не задан — принят не северный (жилые от 2,5 м) (К-7).
Знак «**» — предложение проектировщика, заказчиком не утверждено (согласовать с заказчиком): записи в реестре нет: ЩС — щит слаботочный: место и состав.
См. лист открытых вопросов (лист 7, записи К-1, К-2, К-4, К-7).

Изм.	Кол.уч	Лист	№ док.	Подп.	Дата
Разраб.		Кырлан А.С.			21.10.26
Пров.					
ГИП					
Н. контр.					
Утв.					

ГД-2026-010-АИ

Дом 331 м²

Общая площадь 270,67* м² · * размеры приняты, не замерены (реестр — л. 7, К-1)

Дизайн-проект интерьера

Стадия	Лист	Листов
РП	154	159

Ведомость объёмов работ (окончание)

М б/м

Кырлан Александр Сергеевич

выпуск 18.10.2026 № 9365d64cec · стр. 161 из 197

Спецификация материалов

Отделочные материалы: чистое количество, запас, упаковка, к заказу · ГОСТ 21.110-2013

ПРЕДВАРИТЕЛЬНО · не для производства работ · открыто пунктов: 6 (реестр — л. 7)

Спецификация материалов (ГОСТ 21.110-2013, форма 1)

Поз.	Наименование и техническая характеристика	Тип, марка, артикул	Код продукции	Поставщик	Ед. изм.	Количество				Масса ед., кг	Примечание
						чистое	запас, %	упаковка	к заказу		
Покрытия полов и облицовка											
1	Инженерная доска (дуб натуральный, рабочий слой 4 мм, эмиссия E1, прямая укладка)	1167-4250			м²	190,07	7	по артикулу	203,40 м²		пом. 1, 2, 5, 6, 7, 13, 14, 16, 17, 18, 19; до целой упаковки; л. 67, 68, 70–72
2	Клей для паркетной и инженерной доски (эластичный, по ТУ изготовителя доски)	по выбору подрядчика			м²	190,07		ведро по ТУ	по ТУ		расход кг/м² — по ТУ клея; л. 67, 68
3	Керамогранит 600×600 мм под травертин	аналог: керамогранит под травертин			шт	53	10	коробка	59 шт		13 целых + 40 с подрезкой; 18,04 м² по раскладке, к заказу 21,24 м²; пом. 3, 15, 20; л. 61–66
4	Керамогранит 600×1200 мм под травертин	аналог: керамогранит под травертин			шт	116	10	коробка	131 шт		40 целых + 76 с подрезкой; 60,56 м² по раскладке, к заказу 94,32 м²; пом. 3, 15, 20; л. 61–66
5	Керамогранит 600×1200 мм A8UZ	A8UZ			шт	82	10	коробка	92 шт		16 целых + 66 с подрезкой; 48,05 м² по раскладке, к заказу 66,24 м²; пом. 4, 8, 9, 11, 12; л. 61–66
Сухие смеси и гидроизоляция											
6	Клей плиточный цементный класса C2 TE S1 (ГОСТ Р 56387-2018)	Ceresit CM 17 или аналог			кг	955,87	10	мешок 25 кг	43 меш.	25	слой 5 мм, 1,50 кг/м² на 1 мм; л. 61
7	Затирка цементная класса CG2WA, цвет — по колерной карте	Mapei Ultracolor Plus 132 или аналог			кг	9,74	10	упак. 2 кг	6 упак.	2	расход (a+b)/ab × шов × t × 1,6 кг/м²; л. 61
8	Гидроизоляция обмазочная полимерная, 2 слоя, лента в углах, манжеты на выводах	по выбору подрядчика			м²	39,20	10	ведро по ТУ	по ТУ		пом. 3, 15, 20; расход кг/м² — по ТУ; л. 61
9	Лента демпферная по периметру пола из плитки	по выбору подрядчика			м	77,72	10	рулон	86,00 м		л. 61
10	Смесь цементно-песчаная для стяжки М200 (53 мм, 50 мм, 33 мм, 55 мм, 61 мм)	по выбору подрядчика			м³	14,09	5	мешок по ТУ	по ТУ		S 273,81 м² × толщина; армирование и маяки — по ТУ; л. 67, 68
11	Смесь штукатурная гипсовая для машинного и ручного нанесения по маякам, слой до 10 мм	по выбору подрядчика			м²	674,24	10	мешок по ТУ	по ТУ		пом. 1, 2, 3, 4, 5, 6, 7, 8, 9, 10, 11, 12, 13, 14, 15, 16, 17, 18, 19, 20; расход кг/м² на 1 мм слоя — по ТУ смеси, толщина — по замеру кривизны стен; л. 15, 16, 70–72
Короба из ГКЛВ											
12	Лист ГКЛВ 12,5 мм, 2500 × 1200 мм, обшивка коробов в 2 слоя	по выбору подрядчика			м²	9,68	10	лист 3,00 м²	4,00 лист		инсталляция пом. 3: 1,64 м²; инсталляция пом. 15: 1,73 м²; инсталляция пом. 20: 1,47 м²; площадь × 2 слоя; короб К1 над полом — в спецификации ВК; л. 49, 50, 61–66
13	Профиль стальной оцинкованный 27 × 28 мм: каркас коробов (стойки и направляющие)	по выбору подрядчика			м	23,98	10	хлыст 3 м	9 шт		стойки через 400 мм по свободному периметру + направляющие по полу и потолку; крепёж, лента, шпаклёвка швов — по узлу короба; л. 49, 50, 61–66
Слаботочные сети											
14	Кабель домофона — тип по системе поставщика	по выбору подрядчика			м	2,80		бухта по ТУ	3,00 м		по лучам от ЩС**, 1 точ., запас 10 % уже в длине; 2 точ. — предложение листа слаботочки (знак «*» на плане); л. 43, 44
15	Кабель коаксиальный RG-6 (75 Ом) к розеткам ТВ	по выбору подрядчика			м	70,60		бухта по ТУ	71,00 м		по лучам от ЩС**, 5 точ., запас 10 % уже в длине; 2 точ. — предложение листа слаботочки (знак «*» на плане); л. 43, 44

Допущения и предложения на листе

Основа листа: размеры и контуры этажей подобраны проектировщиком по составу помещений и площадям этажей с картинки 470 px (размеры на ней не читаются); обмер и исходный проект — задание (К-1); высоты: 1-й этаж 2800 мм, мансарда 2700 мм (горизонтальная часть) приняты; скаты кровли мансарды приняты по картинке: колено 1200 мм, уклон 45°, конёк вдоль длинной стороны; проект КР — задание (К-2); наружные стены 400 мм, перегородки 120 мм приняты (К-1); разрешённая мощность 15 кВт принята по типовым ТУ для частного дома (К-4); подрайон климата не задан — принят не северный (жилые от 2,5 м) (К-7).

Знак «**» — предложение проектировщика, заказчиком не утверждено (согласовать с заказчиком): записи в реестре нет: ЩС — щит слаботочный: место и состав; плинтус пом. 1, 2, 4–14, 16, 17, фартук пом. 1, акцент пом. 5 — артикул изделия не выбран: позиция описана характеристиками («аналог по характеристикам»), артикул выбирается при закупке; пол пом. 10 — покрытие пола гаража — предложение исполнителя: выдерживает шины, масло и антигололёдные реагенты, без швов.

См. лист открытых вопросов (лист 7, записи К-1, К-2, К-4, К-7).

Изм.	Кол.уч	Лист	№ док.	Подп.	Дата
Разраб.		Кырлан А.С.			21.10.26
Пров.					
ГИП					
Н. контр.					
Утв.					

ГД-2026-010-АИ

Дом 331 м²

Общая площадь 270,67* м² · * размеры приняты, не замерены (реестр — л. 7, К-1)

Дизайн-проект интерьера

Стадия	Лист	Листов
РП	155	159

Спецификация материалов

М б/м

Кырлан Александр Сергеевич

Спецификация материалов (продолжение)

Отделочные материалы: чистое количество, запас, упаковка, к заказу · ГОСТ 21.110-2013

Спецификация материалов (ГОСТ 21.110-2013, форма 1) (продолжение)

Поз.	Наименование и техническая характеристика	Тип, марка, артикул	Код продукции	Поставщик	Ед. изм.	Количество				Масса ед., кг	Примечание
						чистое	запас, %	упаковка	к заказу		
16	Кабель U/UTP кат. 5e (LAN, Wi-Fi и камеры по PoE)	по выбору подрядчика			м	11,90		бухта по ТУ	12,00 м		по лучам от ЩС**, 1 точ., запас 10 % уже в длине; 2 точ. — предложение листа слаботочки (знак «*» на плане); л. 43, 44
17	Кабель U/UTP кат. 6 (LAN, Wi-Fi и камеры по PoE)	по выбору подрядчика			м	96,40		бухта по ТУ	97,00 м		по лучам от ЩС**, 7 точ., запас 10 % уже в длине; 2 точ. — предложение листа слаботочки (знак «*» на плане); л. 43, 44
18	Гофротруба Ø20 для слаботочных линий, отдельно от силовых	по выбору подрядчика			м	163,50		бухта по ТУ	164,00 м		по длине лучей без участков в канале плинтуса (≈ 90 %); л. 43, 44
19	Розетка компьютерная RJ45, кат. 6, с рамкой и подрозетником	по выбору подрядчика			шт	7		шт	7 шт		LAN1, LAN2, LAN3**; серия механизмов — как у розеток и выключателей; л. 37, 38, 43, 44
20	Розетка телевизионная (коаксиальная) с рамкой и подрозетником	по выбору подрядчика			шт	5		шт	5 шт		ТВ1, ТВ2; серия механизмов — как у розеток и выключателей; л. 37, 38, 43, 44
21	Трубка или монитор домофона (поставка домофонной организации)	по выбору подрядчика			шт	1		шт	1 шт		ДФ1; серия механизмов — как у розеток и выключателей; л. 37, 38, 43, 44
22	Щит слаботочный ЩС**: корпус, DIN-рейка, розетки 220 В	по выбору подрядчика			шт	1		шт	1 шт		ЩС**; серия механизмов — как у розеток и выключателей; л. 37, 38, 43, 44
23	Патч-панель, портов не менее 8	по выбору подрядчика			шт	1		шт	1 шт		серия механизмов — как у розеток и выключателей; л. 37, 38, 43, 44
Лакокрасочные материалы											
24	Краска интерьерная акриловая, полуматовая, класс истирания 1	Tikkurila Luja 7 S 0804-Y30R «S 0804-Y30R»			л	27,43	10	банка 2,7 л	12 банк		114,30 м² × 2 сл. × 0,12 л/м²; пом. 1, 11, 12; л. 70–72
25	Краска интерьерная акриловая, матовая, класс истирания 1	Tikkurila Luja 7 S 0804-Y30R «S 0804-Y30R»			л	11,95	10	банка 2,7 л	5 банк		49,81 м² × 2 сл. × 0,12 л/м²; пом. 1 (пот.), 11 (пот.), 12 (пот.); л. 70–72
26	Краска интерьерная акриловая, матовая, класс истирания 1	Farrow & Ball Modern Emulsion No. 298 «Bancha»			л	1,36	10	банка 2,5 л	1 банк		5,68 м² × 2 сл. × 0,12 л/м²; пом. 2; л. 70–72
27	Краска интерьерная акриловая, матовая, класс истирания 1	Farrow & Ball Modern Emulsion No. 226 «Joa's White»			л	78,23	10	банка 2,5 л	35 банк		325,94 м² × 2 сл. × 0,12 л/м²; пом. 2, 4, 6, 8, 9, 10, 13, 16, 17, 18, 19; л. 70–72
28	Краска интерьерная акриловая, глубокоматовая, класс истирания 2	Tikkurila Anti-Reflex 2 No. 105 «Slaked Lime»			л	46,63	10	банка 2,7 л	19 банк		194,30 м² × 2 сл. × 0,12 л/м²; пом. 2 (пот.), 4 (пот.), 6 (пот.), 7 (пот.), 8 (пот.), 9 (пот.), 10 (пот.), 13 (пот.), 14 (пот.), 16 (пот.), 17 (пот.), 18 (пот.), 19 (пот.); л. 70–72
29	Краска интерьерная акриловая, матовая, класс истирания 1	Tikkurila Luja 7 No. 105 «Slaked Lime»			л	4,33	10	банка 2,7 л	2 банк		18,04 м² × 2 сл. × 0,12 л/м²; пом. 3 (пот.), 15 (пот.), 20 (пот.); л. 70–72
30	Краска интерьерная акриловая, матовая, класс истирания 2	Tikkurila Optiva 5 Matt No. 93 «Studio Green — почти чёрный зелёный»			л	4,65	10	банка 2,7 л	2 банк		12,92 м² × 3 сл. × 0,12 л/м²; пом. 5; л. 70–72
31	Краска интерьерная акриловая, матовая, класс истирания 2	Tikkurila Optiva 5 Matt S 0804-Y30R «S 0804-Y30R»			л	7,73	10	банка 2,7 л	4 банк		32,20 м² × 2 сл. × 0,12 л/м²; пом. 5; л. 70–72
32	Краска интерьерная акриловая, глубокоматовая, класс истирания 2	Tikkurila Anti-Reflex 2 S 0804-Y30R «S 0804-Y30R»			л	8,10	10	банка 2,7 л	4 банк		33,74 м² × 2 сл. × 0,12 л/м²; пом. 5 (пот.); л. 70–72
33	Краска интерьерная акриловая, матовая, класс истирания 1	Tikkurila Harmony No. 105 «Slaked Lime»			л	10,07	10	банка 2,7 л	5 банк		41,96 м² × 2 сл. × 0,12 л/м²; пом. 7, 14; л. 70–72
34	Краска интерьерная акриловая, матовая, класс истирания 1	Farrow & Ball Modern Emulsion S 7020-G10Y «Хвойный тёмно-зелёный»			л	1,82	10	банка 2,5 л	1 банк		7,60 м² × 2 сл. × 0,12 л/м²; пом. 13; л. 70–72

Допущения и предложения на листе

Основа листа: размеры и контуры этажей подобраны проектировщиком по составу помещений и площадям этажей с картинки 470 px (размеры на ней не читаются); обмер и исходный проект — задание (К-1); высоты: 1-й этаж 2800 мм, мансарда 2700 мм (горизонтальная часть) приняты; скаты кровли мансарды приняты по картинке: колено 1200 мм, уклон 45°, конёк вдоль длинной стороны; проект КР — задание (К-2); наружные стены 400 мм, перегородки 120 мм приняты (К-1); разрешённая мощность 15 кВт принята по типовым ТУ для частного дома (К-4); подрайон климата не задан — принят не северный (жилые от 2,5 м) (К-7).

Знак «**» — предложение проектировщика, заказчиком не утверждено (согласовать с заказчиком): записи в реестре нет: ЩС — щит слаботочный: место и состав; LAN3 — розетка LAN у рабочего стола; плинтус пом. 1, 2, 4–14, 16, 17, фартук пом. 1, акцент пом. 5 — артикул изделия не выбран: позиция описана характеристиками («аналог по характеристикам»), артикул выбирается при закупке; пол пом. 10 — покрытие пола гаража — предложение исполнителя: выдерживает шины, масло и антигололёдные реагенты, без швов.

См. лист открытых вопросов (лист 7, записи К-1, К-2, К-4, К-7).

Изм.	Кол.уч	Лист	№ док.	Подп.	Дата
Разраб.		Кырлан А.С.			21.10.26
Пров.					
ГИП					
Н. контр.					
Утв.					

ГД-2026-010-АИ

Дом 331 м²

Общая площадь 270,67* м² · * размеры приняты, не замерены (реестр — л. 7, К-1)

Дизайн-проект интерьера	Стадия	Лист	Листов
	РП	156	159
Спецификация материалов (продолжение) М б/м	**Кырлан Александр Сергеевич**		

выпуск 18.10.2026 № 9365d64cec · стр. 163 из 197

Спецификация материалов (окончание)

Отделочные материалы: чистое количество, запас, упаковка, к заказу · ГОСТ 21.110-2013

Спецификация материалов (ГОСТ 21.110-2013, форма 1) (продолжение)

Поз.	Наименование и техническая характеристика	Тип, марка, артикул	Код продукции	Поставщик	Ед. изм.	Количество				Масса ед., кг	Примечание
						чистое	запас, %	упаковка	к заказу		
35	Краска интерьерная акриловая, матовая, класс истирания 1	Farrow & Ball Modern Emulsion No. 64 «Red Earth»			л	1,76	10	банка 2,5 л	1 банк		7,35 м² × 2 сл. × 0,12 л/м²; пом. 16; л. 70–72
36	Краска интерьерная акриловая, матовая, класс истирания 1	Farrow & Ball Modern Emulsion S 3020-G30Y «S 3020-G30Y»			л	2,96	10	банка 2,5 л	2 банк		12,33 м² × 2 сл. × 0,12 л/м²; пом. 18; л. 70–72
37	Краска интерьерная акриловая, матовая, класс истирания 1	Farrow & Ball Modern Emulsion S 3040-Y70R «S 3040-Y70R»			л	3,56	10	банка 2,5 л	2 банк		14,85 м² × 2 сл. × 0,12 л/м²; пом. 19; л. 70–72
38	Шпаклёвка финишная полимерная под окраску (стены и потолки, Q3)	по выбору подрядчика			м²	897,26	10	ведро по ТУ	по ТУ		расход кг/м² на слой — по ТУ; л. 70–72
39	Грунтовка акриловая глубокого проникновения, 2 слоя	по выбору подрядчика			м²	970,13	10	канистра по ТУ	по ТУ		расход л/м² — по ТУ; л. 70–72
Погонажные изделия и потолки											
40	Плинтус напольный МДФ под покраску, h=80 мм, крепление к стене	аналог: плинтус МДФ под окраску 80×16 мм			м.п.	36,50	10	хлыст 2,4 м	17 шт		пом. 1, 5; длина хлыста — по артикулу; л. 70–72
41	Плинтус напольный МДФ под покраску, h=80 мм, крепление к стене	аналог: плинтус МДФ под покраску 80×16			м.п.	112,30	10	хлыст 2,4 м	52 шт		пом. 2, 4, 6, 7, 8, 9, 13, 14, 16, 17; длина хлыста — по артикулу; л. 70–72
42	Плинтус напольный ПВХ, h=100 мм, крепление к стене	аналог: плинтус ПВХ влагостойкий 100 мм, серый			м.п.	21,98	10	хлыст 2,4 м	11 шт		пом. 10; длина хлыста — по артикулу; л. 70–72
43	Керамогранит на плинтус: полосы h=80 мм из плитки пола, кромка с запилом 45°	аналог: плинтус из керамогранита пола, подрезка 80 мм, верхняя кромка с запилом 45°			м²	2,15	15	из партии пола	2,47 м²		26,84 м.п. × 0,08 м; пом. 11, 12; заказывать целыми плитками одной партии с полом, число плиток — по раскладке плиточника; л. 67, 68, 70–72
44	Плинтус напольный МДФ под покраску, h=69 мм, крепление к стене	SX165			м.п.	32,20	10	хлыст 2,4 м	15 шт		пом. 18, 19; длина хлыста — по артикулу; л. 70–72
45	Потолок подвесной ГКЛ/ГКЛВ по каркасу Knauf П113: листы, профили, подвесы, лента, шпаклёвка швов	Knauf П113			м²	202,89		комплект	по л. потолков		площадь — по ведомости потолков; число листов, профилей и подвесов — по шагам каркаса на листе потолков; л. 55–60

Примечания

1. Чистое количество — из ведомости объёмов работ и раскладки плитки; запас — отдельной графой (доска — по ведомости отделки, плитка, краска и плинтус — 10 %); «к заказу» — с запасом и кратно упаковке.
2. Плитка — штуками по раскладке, запас на каждую поверхность. Калибр (рабочий размер) и тон — одной партией на помещение, калибр указать при заказе и сверить с раскладкой до укладки.
3. Краска — 0,12 л/м² на слой (середина вилки 0,10–0,15 л/м²) по фактической площади окраски из ведомости отделки; колеровка одной партией.
4. «По ТУ» — расход задаёт производитель выбранного продукта; количество к заказу — после выбора марки.
5. Поз. 3, 4, 40, 41, 42, 43 заданы характеристиками («аналог:»): марку, артикул и поставщика согласовать с заказчиком до закупки, без артикула не заказывать.
6. Штукатурная смесь — на ту же площадь, что строка ВОР «Штукатурка стен» (674,24 м²): площадь одна, расход смеси задаёт производитель.
7. Коробы инсталляции и стояков: ГКЛВ в 2 слоя и профиль 27 × 28 мм считаются по свободным граням коробов (источник — раскладка плиточника и шахты в данных); короб К1 над полом — в спецификации ВК.
8. Потолки ГКЛ: в этой спецификации — площадь системы П113; число листов, профилей и подвесов — по шагам каркаса на листе потолков (подвесы через 1000, несущие через 500, основные через 1200 мм), схема каркаса не выпущена. Сантехника, светильники и мебель — по своим спецификациям.

Допущения и предложения на листе

Основа листа: размеры и контуры этажей подобраны проектировщиком по составу помещений и площадям этажей с картинки 470 px (размеры на ней не читаются); обмер и исходный проект — задание (К-1); высоты: 1-й этаж 2800 мм, мансарда 2700 мм (горизонтальная часть) приняты; скаты кровли мансарды приняты по картинке: колено 1200 мм, уклон 45°, конёк вдоль длинной стороны; проект КР — задание (К-2); наружные стены 400 мм, перегородки 120 мм приняты (К-1); разрешённая мощность 15 кВт принята по типовым ТУ для частного дома (К-4); подрайон климата не задан — принят не северный (жилые от 2,5 м) (К-7).

Знак «**» — предложение проектировщика, заказчиком не утверждено (согласовать с заказчиком): записи в реестре нет: плинтус пом. 1, 2, 4–14, 16, 17, фартук пом. 1, акцент пом. 5 — артикул изделия не выбран: позиция описана характеристиками («аналог по характеристикам»), артикул выбирается при закупке; пол пом. 10 — покрытие пола гаража — предложение исполнителя: выдерживает шины, масло и антигололёдные реагенты, без швов.

См. лист открытых вопросов (лист 7, записи К-1, К-2, К-4, К-7).

Изм.	Кол.уч	Лист	№ док.	Подп.	Дата
Разраб.		Кырлан А.С.			21.10.26
Пров.					
ГИП					
Н. контр.					
Утв.					

ГД-2026-010-АИ

Дом 331 м²

Общая площадь 270,67* м² · * размеры приняты, не замерены (реестр — л. 7, К-1)

Дизайн-проект интерьера	Стадия	Лист	Листов
	РП	157	159

Спецификация материалов (окончание)

М б/м

Кырлан Александр Сергеевич

Смета ориентировочная

ПРЕДВАРИТЕЛЬНО · не для производства работ · открыто пунктов: 6 (реестр — л. 7)

Работы, материалы, оборудование, услуги и резерв · цены — ориентир по открытым прайсам, не коммерческое предложение

Сводная смета (прайсы собраны 21.09.2026, часть расценок сверена повторно 24.09.2026, Москва)

№	Наименование работ, материалов, услуг	Ед. изм.	Кол-во	Цена за ед., ₽	Стоимость, ₽			Чей подряд	Срок поставки, дн.	Основание	Источник цены
					план	факт	разница				
Работы — по ведомости объёмов работ											
1	Демонтаж и черновые работы (без 6 поз. по КП)	раздел	1		837 428			бригада, поставщик		ВОР, поз. 1–11; л. 150–154	по ВОР
2	Инженерные системы (без 13 поз. по КП)	раздел	1		297 892			бригада		ВОР, поз. 12–35; л. 150–154	по ВОР
3	Чистовые работы (без 1 поз. по КП)	раздел	1		1 938 641			бригада, поставщик		ВОР, поз. 36–55; л. 150–154	по ВОР
Материалы — по спецификации материалов											
4	Инженерная доска	м²	203,40	4 513	917 944			поставщик		спецификация, поз. 1	Ц7
5	Керамогранит 600×600 мм	м²	21,24	1 800	38 232			поставщик		спецификация, поз. 3	Ц6
6	Керамогранит 600×1200 мм	м²	160,56	3 500	561 960			поставщик		спецификация, поз. 4, 5	Ц6
7	Клей плиточный цементный класса C2 TE S1	меш.	43	1 800	77 400			поставщик		спецификация, поз. 6	Ц7
8	Затирка цементная класса CG2WA	упак.	6	1 000	6 000			поставщик		спецификация, поз. 7	Ц7
9	Краска Tikkurila (Luja 7, Anti-Reflex 2, Optiva 5 Matt, Harmony), банка 2,7 л	банк	53	3 510	186 030			поставщик		спецификация, поз. 24, 25, 28, 29, 30, 31, 32, 33	Ц6
10	Краска Farrow & Ball Modern Emulsion, банка 2,5 л	банк	42	5 800	243 600			поставщик		спецификация, поз. 26, 27, 34, 35, 36, 37	Ц7
11	Плинтус напольный МДФ под покраску	шт	84	368	30 912			поставщик		спецификация, поз. 40, 41, 44	Ц7
12	Керамогранит на плинтус: полосы h=80 мм из плитки пола	м²	2,47	1 800	4 446			поставщик		спецификация, поз. 43	Ц6
13	Прочие материалы с расходом по ТУ (клей для доски, гидроизоляция, демпферная лента, смесь для стяжки, смесь штукатурная гипсовая для машинного и ручного нанесения по маякам, лист гклв 12, профиль стальной оцинкованный 27 × 28 мм: каркас коробов (стойки и направляющие), кабель слаботочки, гофра слаботочки, изделия слаботочки, шпаклёвка, грунтовка, плинтус, каркас и ГКЛ потолков)	компл	1	по КП				поставщик		спецификация, поз. 2, 8, 9, 10, 11, 12, 13, 14, 15, 16, 17, 18, 19, 20, 21, 22, 23, 38, 39, 42, 45	
Оборудование и мебель — поставка по спецификациям											
14	Кухонный гарнитур по проекту кухни, изготовление и монтаж (4–8 нед.)	компл	1	по КП				поставщик	уточн.; ориентир 4–8 нед. от замера	л. 95, 96	
15	Двери скрытого монтажа с коробом под покраску, поставка	шт	9	по КП				поставщик	уточн.; ориентир ≈ 30 дн.	л. 19, 20	

Допущения и предложения на листе

Основа листа: размеры и контуры этажей подобраны проектировщиком по составу помещений и площадям этажей с картинки 470 px (размеры на ней не читаются); обмер и исходный проект — задание (К-1); высоты: 1-й этаж 2800 мм, мансарда 2700 мм (горизонтальная часть) приняты; скаты кровли мансарды приняты по картинке: колено 1200 мм, уклон 45°, конёк вдоль длинной стороны; проект КР — задание (К-2); наружные стены 400 мм, перегородки 120 мм приняты (К-1); разрешённая мощность 15 кВт принята по типовым ТУ для частного дома (К-4); подрайон климата не задан — принят не северный (жилые от 2,5 м) (К-7).

См. лист открытых вопросов (лист 7, записи К-1, К-2, К-4, К-7).

Изм.	Кол.уч	Лист	№ док.	Подп.	Дата
Разраб.		Кырлан А.С.			21.10.26
Пров.					
ГИП					
Н. контр.					
Утв.					

ГД-2026-010-АИ

Дом 331 м²

Общая площадь 270,67* м² · * размеры приняты, не замерены (реестр — л. 7, К-1)

Дизайн-проект интерьера

Стадия	Лист	Листов
РП	158	159

Смета ориентировочная

М б/м

Кырлан Александр Сергеевич

Смета ориентировочная (окончание)

Работы, материалы, оборудование, услуги и резерв · цены — ориентир по открытым прайсам, не коммерческое предложение

ПРЕДВАРИТЕЛЬНО · не для производства работ · открыто пунктов: 6 (реестр — л. 7)

Сводная смета (прайсы собраны 21.09.2026, часть расценок сверена повторно 24.09.2026, Москва) (продолжение)

№	Наименование работ, материалов, услуг	Ед. изм.	Кол-во	Цена за ед., ₽	Стоимость, ₽			Чей подряд	Срок поставки, дн.	Основание	Источник цены
					план	факт	разница				
16	Двери межкомнатные, поставка	шт	4	по КП				поставщик		л. 19, 20	
17	Оборудование заказчика слаботочных сетей: точка доступа wi-fi — 1 шт; коммутатор — 1 шт	компл	1	по КП				заказчик		л. 37, 38	
18	Сантехника, светильники, мебель и предметы интерьера	компл	1	по КП				поставщик		л. 53; л. 54; л. 99; л. 26–30	
Прочие работы и услуги											
19	Вынос и вывоз строительного мусора	м³		по факту				бригада		после демонтажа	
20	Подъём материалов на этаж (лифтом или вручную — по договору)	т		по факту				бригада		по массе поставки	
21	Доставка чистовых материалов, 10 % от поставки			10 %	206 652			поставщик		от суммы материалов	
22	Уборка после ремонта	м²	270,67	по факту				бригада		S квартиры	
	Итого работы				**3 073 961**						
	Итого материалы				**2 066 524**						
	Итого прочие услуги				**206 652**						
	Резерв на непредвиденные работы и материалы, 15 %				**802 071**						
	ВСЕГО ориентировочно (без оборудования и позиций по КП)				**6 149 208**						

Примечания

1. Смета ориентировочная, не коммерческое предложение: объёмы — из ведомости объёмов работ и спецификации материалов, цены — нижняя граница открытых прайсов Москвы (прайсы собраны 21.09.2026, часть расценок сверена повторно 24.09.2026); перед договором цены подтвердить у подрядчика и поставщиков.
2. Источники цен: Ц1 — Домашний мастерок: прайс на отделочные работы, 2026; Ц2 — Домашний мастерок: прайс на плиточные работы, 2026; Ц3 Домашний мастерок: прайс на электромонтажные работы, 2026; Ц4 — Профи ремонтник: штукатурно-малярные работы; Ц5 — Profi.ru: укладка керамогранита на стены, Москва 2026; Ц6 — knowledge/spec-materials.md, разд. 1 и 3: ориентир по сегментам; Ц7 — Розница Москвы, 09.2026: Лемана ПРО, KGSnab, официальный дилер Farrow & Ball.
3. Повторная сверка с прайсом: 24.09.2026 — плинтус из керамогранита, нарезка плинтуса из плитки; остальные расценки — по прайсам, собранным 21.09.2026.
4. В итог не вошли позиции «по КП» и «по факту»: оборудование и мебель, двери, материалы с расходом по ТУ, вывоз мусора, подъём и уборка.
5. Доставка — 10 % от материалов, резерв — 15 % (частный ремонт 10–20 %) отдельными строками, в количествах не спрятаны. Графы «факт» и «разница» заполняются по актам.

Допущения и предложения на листе

Основа листа: размеры и контуры этажей подобраны проектировщиком по составу помещений и площадям этажей с картинки 470 px (размеры на ней не читаются); обмер и исходный проект — задание (К-1); высоты: 1-й этаж 2800 мм, мансарда 2700 мм (горизонтальная часть) приняты; скаты кровли мансарды приняты по картинке: колено 1200 мм, уклон 45°, конёк вдоль длинной стороны; проект КР — задание (К-2); наружные стены 400 мм, перегородки 120 мм приняты (К-1); разрешённая мощность 15 кВт принята по типовым ТУ для частного дома (К-4); подрайон климата не задан — принят не северный (жилые от 2,5 м) (К-7).
См. лист открытых вопросов (лист 7, записи К-1, К-2, К-4, К-7).

Изм.	Кол.уч	Лист	№ док.	Подп.	Дата
Разраб.		Кырлан А.С.			21.10.26
Пров.					
ГИП					
Н. контр.					
Утв.					

ГД-2026-010-АИ

Дом 331 м²

Общая площадь 270,67* м² · * размеры приняты, не замерены (реестр — л. 7, К-1)

Дизайн-проект интерьера	Стадия	Лист	Листов
	РП	159	159

Смета ориентировочная (окончание)	Кырлан Александр Сергеевич
М б/м	

06

Визуализации

Кырлан Александр Сергеевич

выпуск 18.10.2026 · № 9365d64cec · стр. 167 из 197

3d-top-et1

Дом 331 м² · визуализация 1 из 30

выпуск 18.10.2026 № 9365d64cec · стр. 168 из 197

3d-top-et2

Дом 331 м² · визуализация 2 из 30

выпуск 18.10.2026 № 9365d64cec · стр. 169 из 197

room-balcony1-wC

выпуск 18.10.2026 № 9365d64cec · стр. 170 из 197

выпуск 18.10.2026 № 9365d64cec · стр. 171 из 197

room-balcony2-wide

room-bath1-wide

Дом 331 м² · визуализация 5 из 30

выпуск 18.10.2026 № 9365d64cec · стр. 172 из 197

room-bath2-wide

Дом 331 м² · визуализация 6 из 30

room-bath3-wide

Дом 331 м² · визуализация 7 из 30

выпуск 18.10.2026 № 9365d64cec · стр. 174 из 197

room-bedroom1-wA

Дом 331 м² · визуализация 8 из 30

выпуск 18.10.2026 № 9365d64cec · стр. 175 из 197

room-bedroom1-wC

выпуск 18.10.2026 № 9365d64cec · стр. 176 из 197

room-bedroom2-wA

Дом 331 м² · визуализация 10 из 30

room-bedroom2-wB

room-corridor1-wide

Дом 331 м² · визуализация 12 из 30

выпуск 18.10.2026 № 9365d64cec · стр. 179 из 197

room-corridor2-wide

Дом 331 м² · визуализация 13 из 30

выпуск 18.10.2026 № 9365d64cec · стр. 180 из 197

room-hall1-wA

Дом 331 м² · визуализация 14 из 30

выпуск 18.10.2026 № 9365d64cec · стр. 181 из 197

room-hall1-wB

Дом 331 м² · визуализация 15 из 30

выпуск 18.10.2026 № 9365d64cec · стр. 182 из 197

выпуск 18.10.2026 № 9365d64cec · стр. 183 из 197

room-kids1-wA

room-kids1-wC

room-kids2-wA

Дом 331 м² · визуализация 18 из 30

выпуск 18.10.2026 № 9365d64cec · стр. 185 из 197

выпуск 18.10.2026 № 9365d64cec · стр. 186 из 197

room-kids2-wC

room-kitchen-wA

Дом 331 м² · визуализация 20 из 30

выпуск 18.10.2026 № 9365d64cec · стр. 187 из 197

room-kitchen-wD

Дом 331 м² · визуализация 21 из 30

выпуск 18.10.2026 № 9365d64cec · стр. 188 из 197

room-living-wA

Дом 331 м² · визуализация 22 из 30

выпуск 18.10.2026 № 9365d64cec · стр. 189 из 197

выпуск 18.10.2026 № 9365d64cec · стр. 190 из 197

room-living-wC

room-living-wD

Дом 331 м² · визуализация 24 из 30

выпуск 18.10.2026 № 9365d64cec · стр. 191 из 197

выпуск 18.10.2026 № 9365d64cec · стр. 192 из 197

room-storage1-wide

room-storage2-wide

Дом 331 м² · визуализация 26 из 30

выпуск 18.10.2026 № 9365d64cec · стр. 193 из 197

room-storage3-wide

Дом 331 м² · визуализация 27 из 30

выпуск 18.10.2026 № 9365d64cec · стр. 194 из 197

выпуск 18.10.2026 № 9365d64cec · стр. 195 из 197

room-study-wA

room-study-wD

room-wardrobe-wide

Дом 331 м² · визуализация 30 из 30

выпуск 18.10.2026 № 9365d64cec · стр. 197 из 197