ДИЗАЙН-ПРОЕКТ ИНТЕРЬЕРА

Квартира с кабинетом

современный модерн

127,29 м²

природность · плавность · камерность · ремесленность · поэтичность · приглушённая цветность · сумеречный тёплый свет

Современный модерн 2026: модерн 60 % + современный (contemporary.json) 40 %. Стены — Bone No. 15 и льняной беж S 2010-Y30R, потолки — Winter V503, шалфей Calke Green No. 34 и пудровый Peignoir No. 286 вторым планом, акценты павлиний S 5030-B10G (бархат), горчица India Yellow No. 66, морёный дуб S 8010-Y30R; металл — латунь.

ПАЛИТРА 60 / 30 / 10

F&B No. 15	NCS S 2010-Y30R	V503	F&B No. 34	F&B No. 286
60 %	60 %	60 %	30 %	30 %

АВТОР ПРОЕКТА

Кырлан Александр Сергеевич

Октябрь 2026



Визуализация 1 · Вид сверху (3D): планировка с мебелью, текстилем и декором

ОБЪЕКТ	ОБЩАЯ ПЛОЩАДЬ	ПОМЕЩЕНИЙ
Квартира с кабинетом	127,29 м²	9, из них жилых 4
СТИЛЬ	**СТАДИЯ**	**ШИФР**
Модерн (ар-нуво) · современный модерн	Рабочий проект	ГД-2026-008-АИ

КАК ОСТАВИТЬ ПРАВКУ

Нажмите кнопку «Правка к этому листу» в правом верхнем углу любого листа — лист откроется на сайте студии: отметьте место на чертеже и наговорите замечание голосом или напишите текстом.

Или откройте все листы проекта:

alex1986-rgb.github.io/linea-design-studio/review.html?p=gost-modern4k

					Проект: Квартира с кабинетом			
	Лист	№ док.	Подпись	Дата	Титульный лист	Стадия	Лист	Листов
Дизайнер	Кырлан А.С.			21.10.26		П	1	97

выпуск 18.10.2026 № 918b20bf25 · стр. 1 из 97

Правка к этому листу

Список листов

Лист	Наименование
1	Титульный лист
2	Список листов
3	План планировки от заказчика
4	План монтажный
5	Кухня (пом. 4). Монтажная схема
6	Шкафы. Монтажная схема. Лист 1 из 2
7	Шкафы. Монтажная схема. Лист 2 из 2
8	Карта покрытий стен
9	Колерная карта
10	План размещения мебели и оборудования
11	Спецификация мебели и оборудования
12	Спецификация мебели и оборудования (продолжение)
13	Спецификация мебели и оборудования (продолжение)
14	Ведомости изделий, техники и фурнитуры
15	План выводов сантехники
16	Схема разводки водопровода и канализации
17	Спецификация сантехнического оборудования
18	Раскладка плитки. Ванная. Развёртки стен
19	Раскладка плитки. Санузел гостевой. Развёртки стен
20	План размещения дверей
21	План потолков
22	План розеток и электровыводов
23	План слаботочных сетей
24	План освещения
25	Спецификация светильников и сценарии освещения
26	Управление светильниками
27	План вентиляции
28	План отопления
29	План покрытий пола
30	Раскладка плитки. Планы полов
31	Раскладка плитки. Прихожая. Фартук кухни
32	Визуализация. Вид сверху
33	Визуализация спальни
34	Визуализация спальни
35	Визуализация спальни
36	Развёртка стены А. Спальня (пом. 1)
37	Развёртка стены Б. Спальня (пом. 1)
38	Развёртка стены В. Спальня (пом. 1)
39	Развёртка стены Г. Спальня (пом. 1)
40	Визуализация: Гардеробная-постирочная
41	Развёртки стен А, Б. Гардеробная-постирочная (пом. 2)
42	Развёртки стен В, Г. Гардеробная-постирочная (пом. 2)
43	Визуализация кабинета
44	Визуализация кабинета
45	Визуализация кабинета
46	Развёртка стены А. Кабинет (пом. 3)
47	Развёртка стены Б. Кабинет (пом. 3)
48	Развёртка стены В. Кабинет (пом. 3)
49	Развёртка стены Г. Кабинет (пом. 3)
50	Визуализация кухни-гостиной
51	Визуализация кухни-гостиной
52	Визуализация кухни-гостиной
53	Визуализация кухни-гостиной
54	Развёртка стены Г. Кухня-гостиная (пом. 4), кухонный фронт
55	Развёртка стены А. Кухня-гостиная (пом. 4), кухонный фронт
56	Развёртка стены Б. Кухня-гостиная (пом. 4)
57	Развёртка стены В. Кухня-гостиная (пом. 4)
58	Визуализация коридора
59	Развёртка стены А1. Коридор (пом. 5)
60	Развёртка стены А2. Коридор (пом. 5)
61	Развёртка стены В. Коридор (пом. 5)
62	Развёртка стены Г. Коридор (пом. 5)
63	Визуализация детской
64	Визуализация детской
65	Визуализация детской
66	Развёртка стены А. Детская (пом. 6)
67	Развёртка стены Б. Детская (пом. 6)
68	Развёртка стены В. Детская (пом. 6)
69	Развёртка стены Г. Детская (пом. 6)
70	Визуализация ванной
71	Визуализация ванной
72	Визуализация ванной
73	Развёртка стены А. Ванная (пом. 7)
74	Развёртка стены Б. Ванная (пом. 7)
75	Развёртка стены В. Ванная (пом. 7)
76	Развёртка стены Г. Ванная (пом. 7)
77	Визуализация прихожей
78	Визуализация прихожей
79	Визуализация прихожей
80	Развёртка стены Б. Прихожая (пом. 8)
81	Развёртка стены В. Прихожая (пом. 8)
82	Развёртка стены Г. Прихожая (пом. 8)
83	Визуализация: Санузел гостевой
84	Визуализация: Санузел гостевой
85	Развёртка стены А. Санузел гостевой (пом. 9)
86	Развёртки стен Б, В. Санузел гостевой (пом. 9)
87	Развёртка стены Г. Санузел гостевой (пом. 9)
Д_1	Система хранения M_06
Д_2	Система хранения M_07
Д_3	Шкаф распашной M_08
Д_4	Шкаф распашной M_24
Д_5	Шкаф распашной M_25
Д_6	Шкаф-купе M_28
Д_7	Кухня (пом. 4). Развёртка гарнитура
С1	Ведомость отделки помещений
С2	Спецификация отделочных материалов
С3	Узлы

Общие указания

1. Размеры даны в мм от чистовых поверхностей стен: слой штукатурки 20 мм по блоку и 5 мм шпаклёвки по ГКЛ учтён. Перед заказом встроенной мебели — контрольный обмер после штукатурки.
2. Привязки мебели — от стен и углов помещения, а не от другой мебели.
3. Розетки, выводы и выключатели под мебель — см. лист 22 «План розеток и электровыводов»; сантехприборы и выводы воды — лист 15.
4. План расстановки не является документацией для изготовления мебели: изделия — по чертежам мебельщика; покупную мебель заменять только на изделия не больше габарита из спецификации (лист 11).
5. Встроенная мебель «стена в стену» — с зазором 10 мм с каждой стороны или с компенсаторами.
6. Развёртки — вид на стену изнутри помещения, по часовой стрелке; расположение стен на схеме листа развёртки; размеры — в мм по чистовым поверхностям; отметки — в м от ±0,000; высоты H — от чистого пола помещения до оси изделия, у декора — до центра.
7. Красные цепочки — привязки электроточек и выводов: по горизонтали от угла чистовых стен, по вертикали от чистого пола, до оси изделия; звенья короче 3 мм на листе вынесены во второй ярус (ближняя к стене цепочка).
8. У знака электроточки: марка (Р — розетка, S — выключатель, Св — светильник, ЭВ вывод кабеля), ×N — число постов в рамке, гр. — группа щита, H — высота оси от чистого пола, мм; группы по клавишам выключателя — на листе выключателей.
9. Схема мебели, приборов и декора не является технической документацией для производства мебели; габариты — по паспортам изделий.
10. Марки позиций: M_NN — мебель, ОБ_NN — оборудование, С_NN — сантехника; О-N отделка (ведомость отделочных материалов, серия С).
11. Размеры мебели и изделий на заказ уточнить по месту после отделочных работ.

	Лист	№ док.	Подпись	Дата
Дизайнер	Кирлан А.О.			21.10.26

Проект: Квартира с кабинетом

Список листов


Стадия	Лист	Листов
П	2	97

выпуск 18.10.2026 № 918b20bf25 · стр. 2 из 97

Правка к этому листу

Отметки по высоте

±0,000 чистый пол пом. 1–6, 8; отсчёт высот
−0,015 чистый пол пом. 7, 9, ниже на 15 мм
−0,064 верх плиты — расчёт, не замер (задание на обмер)
сущ. пол снимается до плиты; не замерен (задание на обмер)

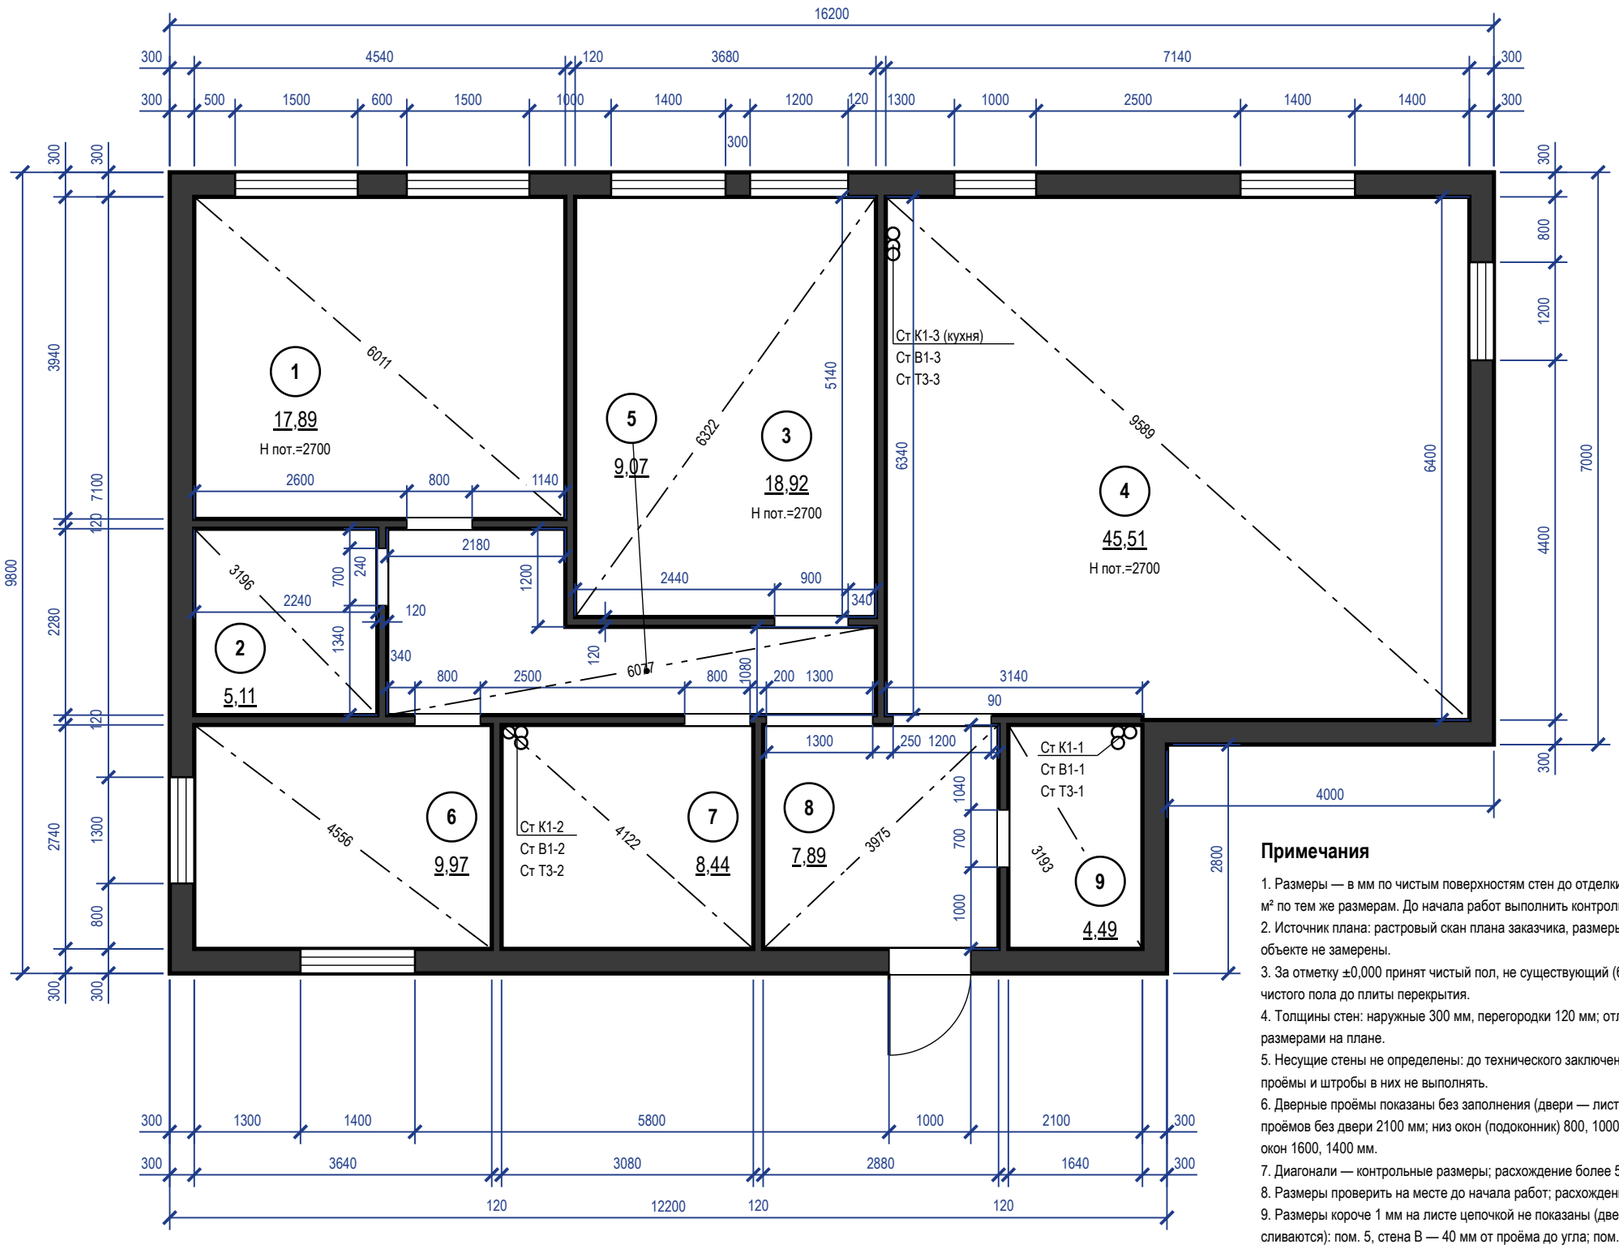

Экспликация помещений

№	Наименование	Площадь, м²
1	Спальня	17,89
2	Гардеробная-постирочная	5,11
3	Кабинет	18,92
4	Кухня-гостиная	45,51
5	Коридор	9,07
6	Детская	9,97
7	Ванная	8,44
8	Прихожая	7,89
9	Санузел гостевой	4,49
	Итого (общая площадь)	**127,29**

Условные обозначения

- существующие стены (сечение)
- окно (рама, остекление)
- проём существующий, без заполнения (откосы)
- стояк: К1 — канализация, В1 — ХВС, Т3 — ГВС
- диагональ помещения — контроль прямоугольности
- (1) номер помещения, площадь м²

Примечания


1. Размеры — в мм по чистым поверхностям стен до отделки (по плану заказчика); площади — в м² по тем же размерам. До начала работ выполнить контрольный обмер.
2. Источник плана: растровый скан плана заказчика, размеры сняты с размерных цепочек, на объекте не замерены.
3. За отметку ±0,000 принят чистый пол, не существующий (блок отметок). Н пот. — высота от чистого пола до плиты перекрытия.
4. Толщины стен: наружные 300 мм, перегородки 120 мм; отличающиеся толщины и уступы размерами на плане.
5. Несущие стены не определены: до технического заключения все стены считать несущими; проёмы и штробы в них не выполнять.
6. Дверные проёмы показаны без заполнения (двери — лист 20); высота дверных проёмов 2100 мм, проёмов без двери 2100 мм; низ окон (подоконник) 800, 1000, 900 мм от чистого пола, высота окон 1600, 1400 мм.
7. Диагонали — контрольные размеры; расхождение более 5 мм подписать на плане как перекос.
8. Размеры проверить на месте до начала работ; расхождение контрольных промеров ≤ 2 %.
9. Размеры короче 1 мм на листе цепочкой не показаны (две выносные линии на таком расстоянии сливаются): пом. 5, стена В — 40 мм от проёма до угла; пом. 8, стена А — 40 мм от угла до проёма.

					Проект: Квартира с кабинетом
	Лист	№ док.	Подпись	Дата	План планировки от заказчика
Дизайнер	Кырлан А.С.			21.10.26	Стадия: П; Лист: 3; Листов: 97

Правка к этому листу

Экспликация помещений

№	Наименование	Площадь, м²
1	Спальня	17,89
2	Гардеробная-постирочная	5,11
3	Кабинет	18,92
4	Кухня-гостиная	45,51
5	Коридор	9,07
6	Детская	9,97
7	Ванная	8,44
8	Прихожая	7,89
9	Санузел гостевой	4,49
	Итого (общая площадь)	**127,29**

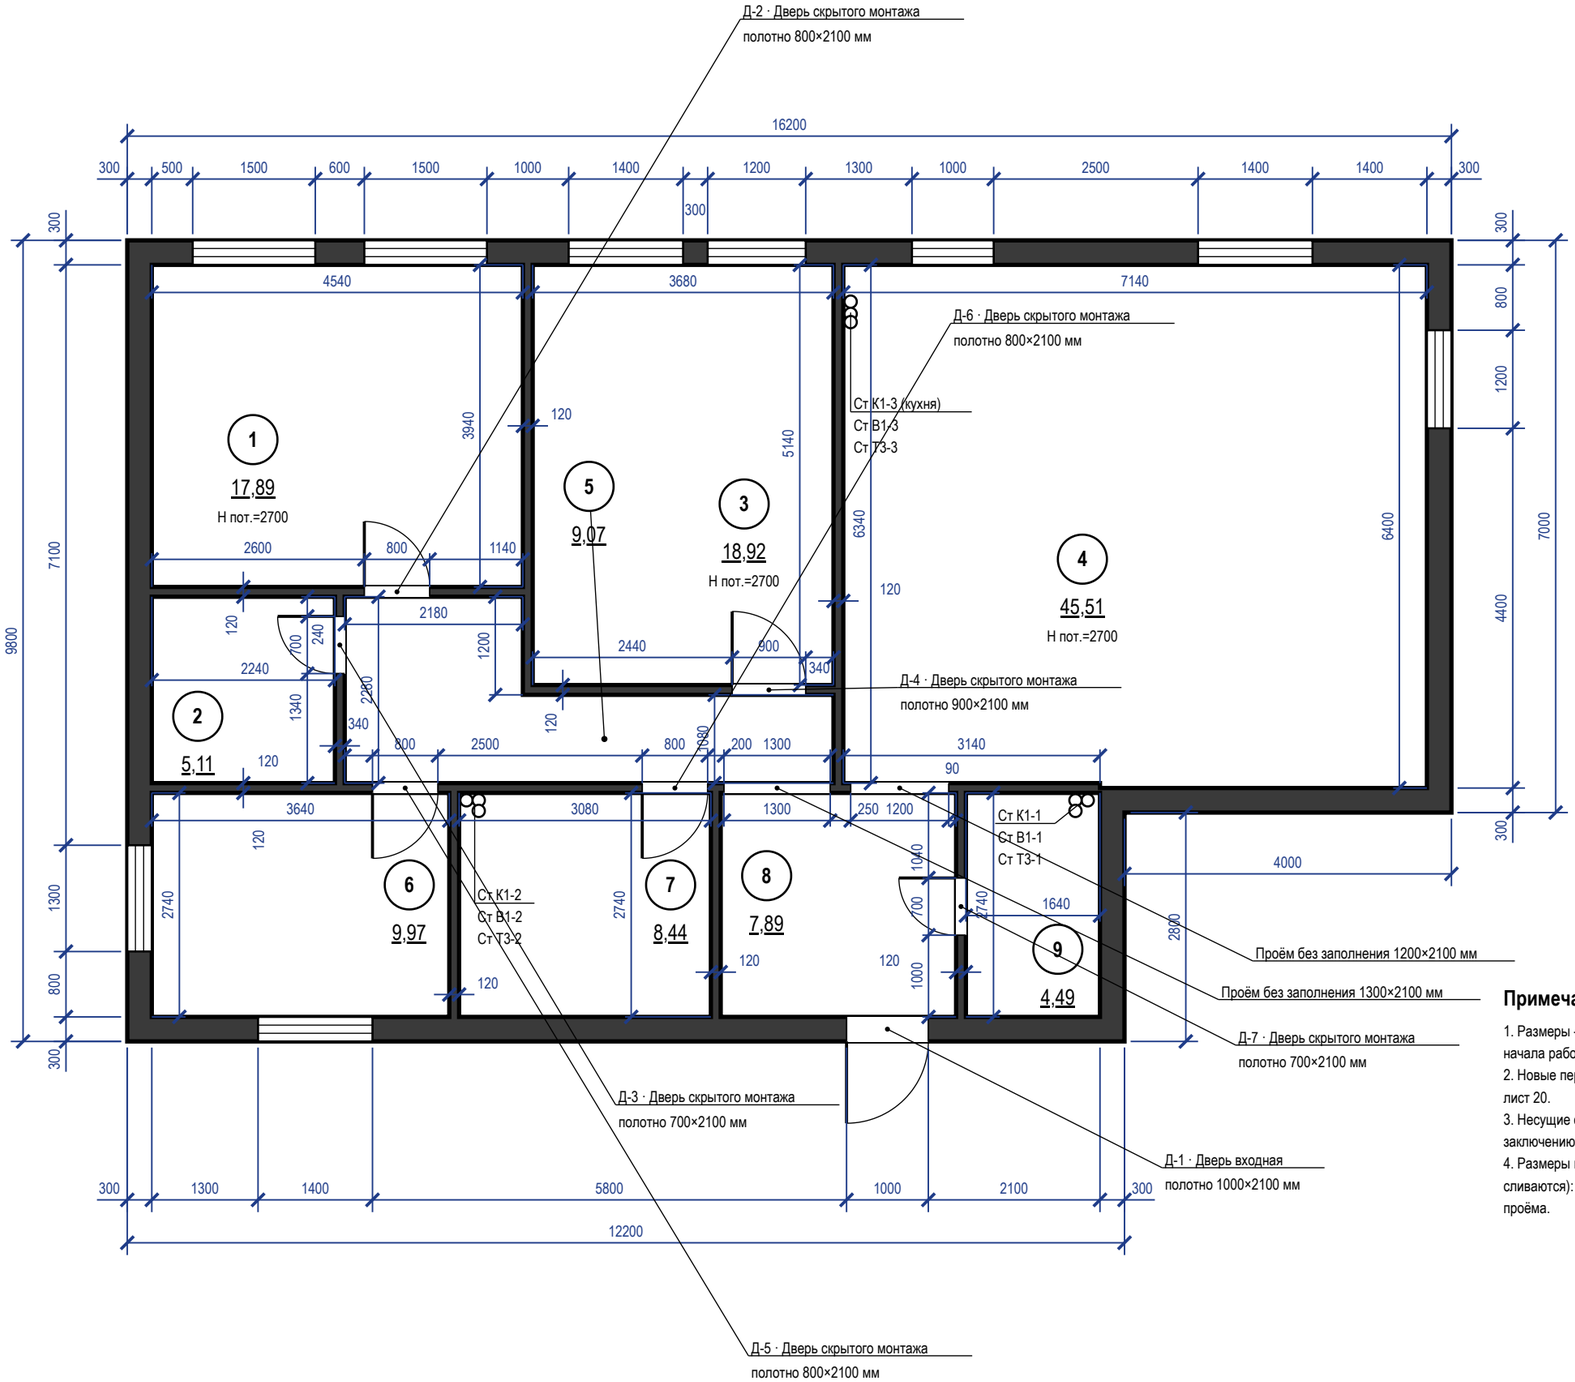

Примечания


1. Размеры — в мм от чистовых поверхностей стен до отделки; размеры уточнить по месту до начала работ.
2. Новые перегородки и облицовки — синим; каркас и обшивка — по выноскам; двери и проёмы лист 20.
3. Несущие стены не изменять: проёмы, ниши и штробы в них — только по техническому заключению.
4. Размеры короче 1 мм на листе цепочкой не показаны (две выносные линии на таком расстоянии сливаются): пом. 5, стена В — 40 мм от проёма до угла; пом. 8, стена А — 40 мм от угла до проёма.

					Проект: Квартира с кабинетом			
	Лист	№ док.	Подпись	Дата	План монтажный	Стадия	Лист	Листов
Дизайнер	Кырлан А.С.			21.10.26		П	4	97


выпуск 18.10.2026 № 918b20bf25 · стр. 4 из 97

Правка к этому листу

Привязка выводов и крепление модулей

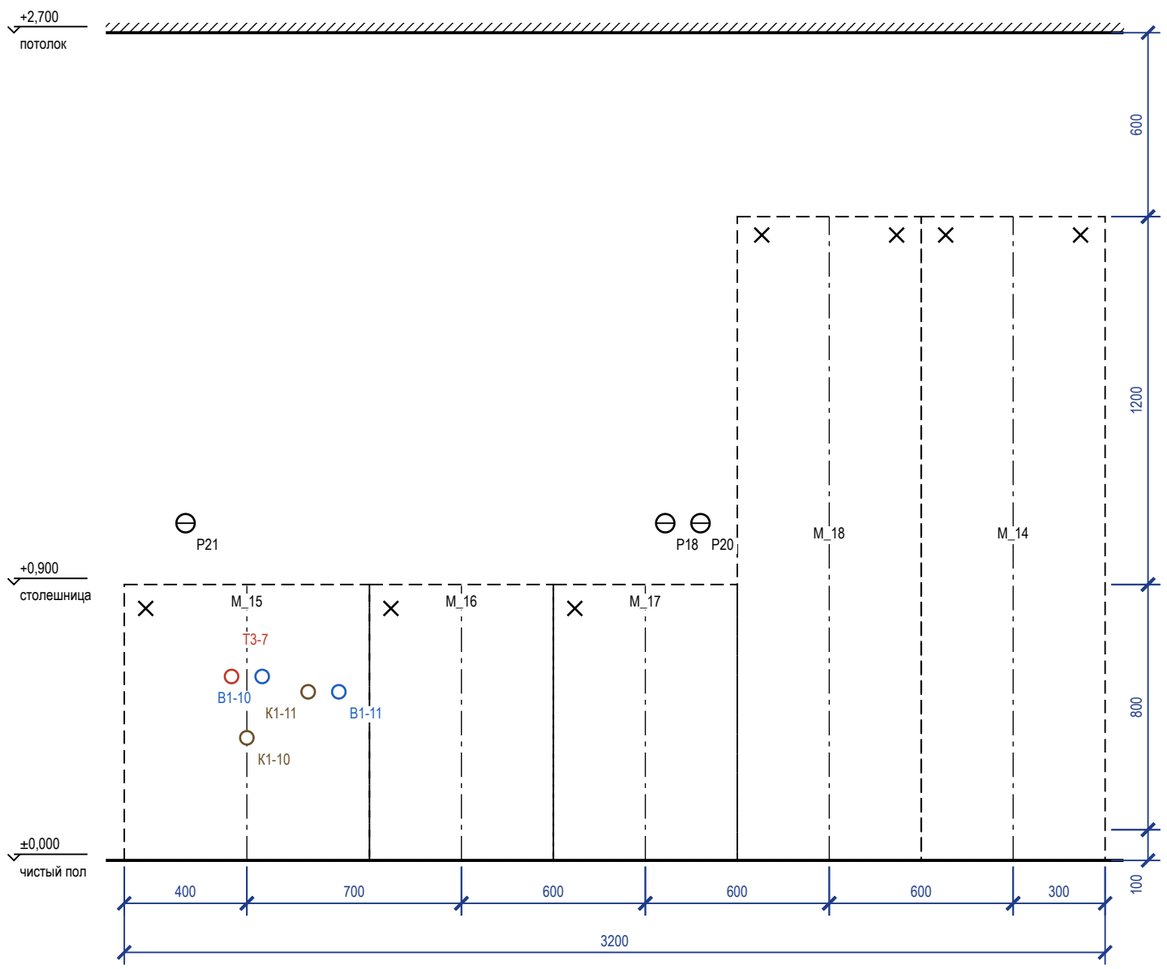

План столешницы

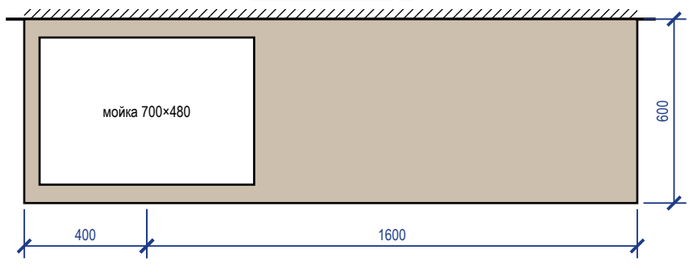

Привязка выводов к осям модулей

Код	Назначение	Модуль	От оси, мм	H, мм	Размещение
P21	розетка — торшер	M_15	−200	1100	над столешницей (фартук)
T3-7	T3 — межос. 100	M_15	−50	600	в модуле мойки
K1-10	K1 Ø50 — мойка	M_15	0	400	в модуле мойки
B1-10	B1 — межос. 100	M_15	+50	600	в модуле мойки
K1-11	K1 Ø40 — слив ПММ в шкафу мойки	M_15	+200	550	в модуле мойки
B1-11	B1 — кран ПММ в шкафу мойки	M_15	+300	550	в модуле мойки
P18	розетка ×2 — ТВ (в одной зоне с TB1, LAN3)	M_17	+65	1100	над столешницей (фартук)
P20	розетка — у ТВ-тумбы	M_17	+180	1100	над столешницей (фартук)

Зазоры под отделку

Поверхность	Отделка	Зазор, мм	Учесть
фартук	керамогранит	10	от чернового основания до корпуса навесных и столешницы
стены	окраска	5	под штукатурку и шпаклёвку за пеналом
пол	инженерная доска		цоколь — после укладки пола, опоры ±20 мм

Условные обозначения

- навесной модуль (невидимый контур)
- ось модуля (от неё — привязка вывода)
- анкер / уголок крепления к стене
- розетка на стене
- вывод кабеля к технике
- B1 — вывод воды B1 / T3, канализации K1

Примечания

1. Выводы — по проекту электрики и ВК; привязка по горизонтали — от оси модуля (плюс — вправо по виду), по высоте — от чистого пола до оси вывода.
2. Пенал — уголки к стене 2 шт. сверху; нижние модули — стяжками между собой и уголком к стене; ряд выставить по уровню опорами цоколя.
3. Розетки над столешницей — не ниже 150 мм над ней и не за корпусом техники; розетка за ПММ, духовым шкафом и холодильником — только в соседнем модуле или в зоне цоколя с доступом.
4. Столешница — вырезы по шаблонам выбранных моделей мойки и варочной панели; торцы у стены — герметик, пристеночный плинтус.


					Проект: Квартира с кабинетом
	Лист	№ док.	Подпись	Дата	
Дизайнер	Кырлан А.С.			21.10.26	Кухня (пом. 4). Монтажная схема

Стадия	Лист	Листов
П	5	97


выпуск 18.10.2026 № 918b20bf25 · стр. 5 из 97

Правка к этому листу


Система хранения M_06 (пом. 2)

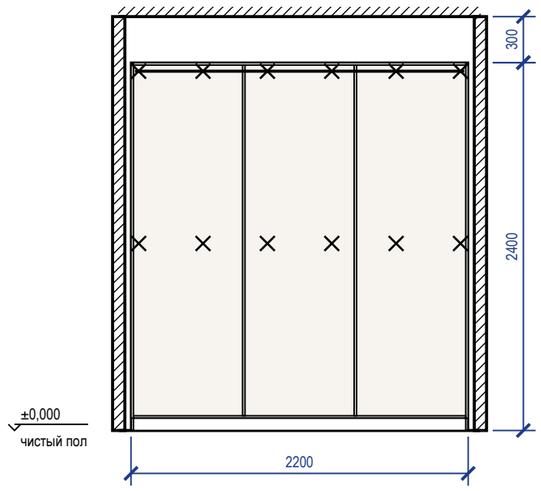

Система хранения M_07 (пом. 2)

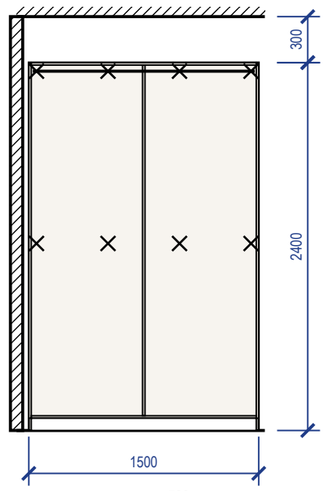

Шкаф распашной M_08 (пом. 3)

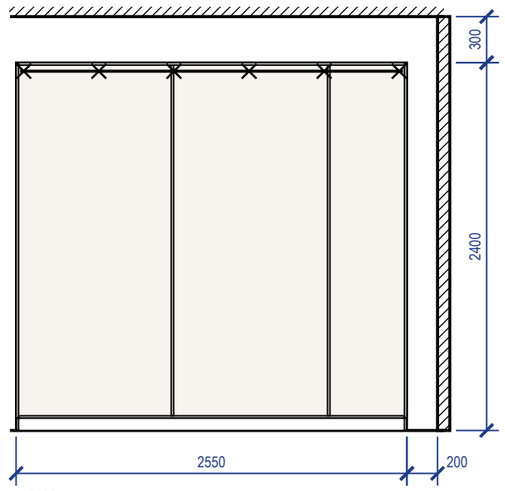

Крепление и зазоры под отделку (изделия листа 1)

Марка	Помещение, стена	Основание	Отделка стены	Зазор, мм	Крепёж по планке	От опрокидывания
M_06	Гардеробная-постирочная (2), стена Г	по основанию — см. таблицу крепежа	окраска	5	анкер 12 шт. (2 ряда)	крепление к стене, 3 точки
M_07	Гардеробная-постирочная (2), стена В	по основанию — см. таблицу крепежа	окраска	5	анкер 8 шт. (2 ряда)	крепление к стене, 3 точки
M_08	Кабинет (3), стена Г	по основанию — см. таблицу крепежа	окраска	5	анкер 6 шт., шаг 490	уголки 2 шт.

Крепёж по основанию стены

Основание стены	Крепёж
бетон, ж/б	анкер-шуруп 7,5×72 или дюбель 8×60 с шурупом 5×70
кирпич полнотелый	дюбель 8×80 с шурупом 5×90
газобетон, пазогребень	дюбель для газобетона 10×100 или химический анкер
гипсокартон	закладная до обшивки (брус 40×80 или фанера 18 мм), саморез в закладную

Условные обозначения

- анкер / уголок крепления к стене
- корпус и полки ЛДСП (вид на стену)
- компенсатор — короб до потолка

Примечания

1. Установочные размеры — от чистого пола и чистых стен; перед установкой контрольный замер после отделки.
2. Порядок: корпус выставить по уровню опорами цоколя → закрепить к стене по задней планке → навесить двери и фасады, отрегулировать зазоры → подогнать и закрепить компенсатор.
3. Анкеры — с шагом не более 500 мм, не ближе 50 мм от края планки; на ГКЛ только в закладную, установленную до обшивки.
4. Скрытые коммуникации под анкеры проверить детектором; трассы электрики по плану розеток.
5. Монтажная схема на 2 листах, лист 1 из 2; продолжение — на следующем листе схемы. Условные обозначения, таблица крепежа по основанию и примечания повторены на каждом листе.

	Лист	№ док.	Подпись	Дата
Дизайнер	Кырлан А.С.			21.10.26

Проект: Квартира с кабинетом


Шкафы. Монтажная схема. Лист 1 из 2

Стадия	Лист	Листов
П	6	97


выпуск 18.10.2026 № 918b20bf25 · стр. 6 из 97

Правка к этому листу


Шкаф распашной М_24 (пом. 4)

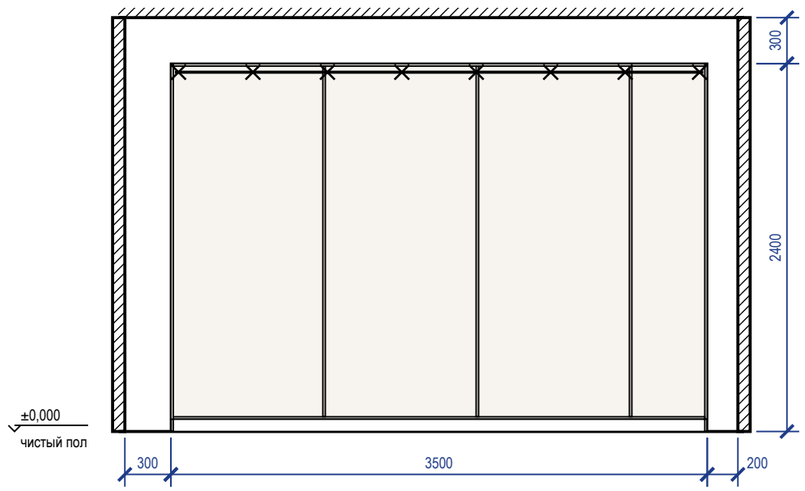

Шкаф распашной М_25 (пом. 6)

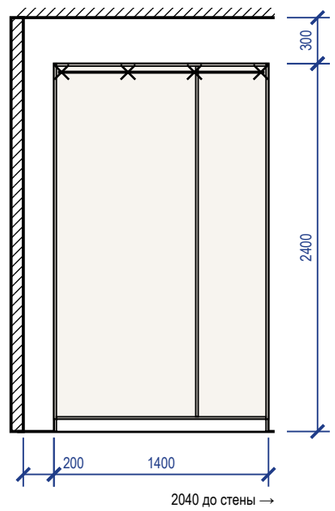

Шкаф-купе М_28 (пом. 8)

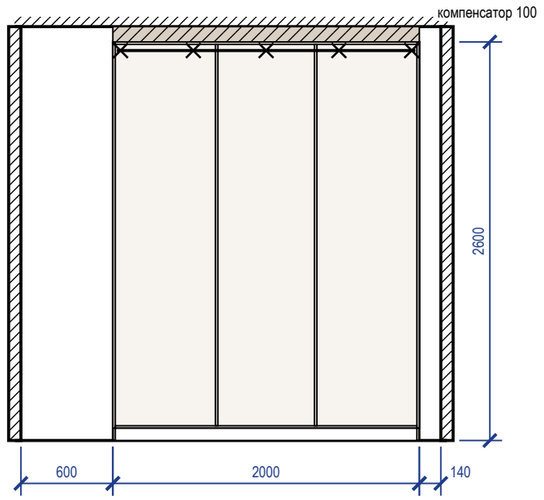

Крепление и зазоры под отделку (изделия листа 2)

Марка	Помещение, стена	Основание	Отделка стены	Зазор, мм	Крепёж по планке	От опрокидывания
М_24	Кухня-гостиная (4), стена В	по основанию — см. таблицу крепежа	окраска	5	анкер 8 шт., шаг 486	уголки 2 шт.
М_25	Детская (6), стена А	по основанию — см. таблицу крепежа	окраска	5	анкер 4 шт., шаг 433	крепление к стене, 2 точки
М_28	Прихожая (8), стена Г	по основанию — см. таблицу крепежа	окраска	5	анкер 5 шт., шаг 475	уголки 2 шт.

Крепёж по основанию стены

Основание стены	Крепёж
бетон, ж/б	анкер-шуруп 7,5×72 или дюбель 8×60 с шурупом 5×70
кирпич полнотелый	дюбель 8×80 с шурупом 5×90
газобетон, пазогребень	дюбель для газобетона 10×100 или химический анкер
гипсокартон	закладная до обшивки (брус 40×80 или фанера 18 мм), саморез в закладную

Условные обозначения

- × — анкер / уголок крепления к стене
- прямоугольник — корпус и полки ЛДСП (вид на стену)
- штриховка — компенсатор — короб до потолка

Примечания


1. Установочные размеры — от чистого пола и чистых стен; перед установкой контрольный замер после отделки.
2. Порядок: корпус выставить по уровню опорами цоколя → закрепить к стене по задней планке → навесить двери и фасады, отрегулировать зазоры → подогнать и закрепить компенсатор.
3. Анкеры — с шагом не более 500 мм, не ближе 50 мм от края планки; на ГКЛ только в закладную, установленную до обшивки.
4. Скрытые коммуникации под анкеры проверить детектором; трассы электрики по плану розеток.
5. Монтажная схема на 2 листах, лист 2 из 2. Условные обозначения, таблица крепежа по основанию и примечания повторены на каждом листе.

					Проект: Квартира с кабинетом
	Лист	№ док.	Подпись	Дата	
Дизайнер	Кырлан А.С.			21.10.26	Шкафы. Монтажная схема. Лист 2 из 2

Стадия	Лист	Листов
П	7	97

выпуск 18.10.2026 № 918b20bf25 · стр. 7 из 97

Правка к этому листу

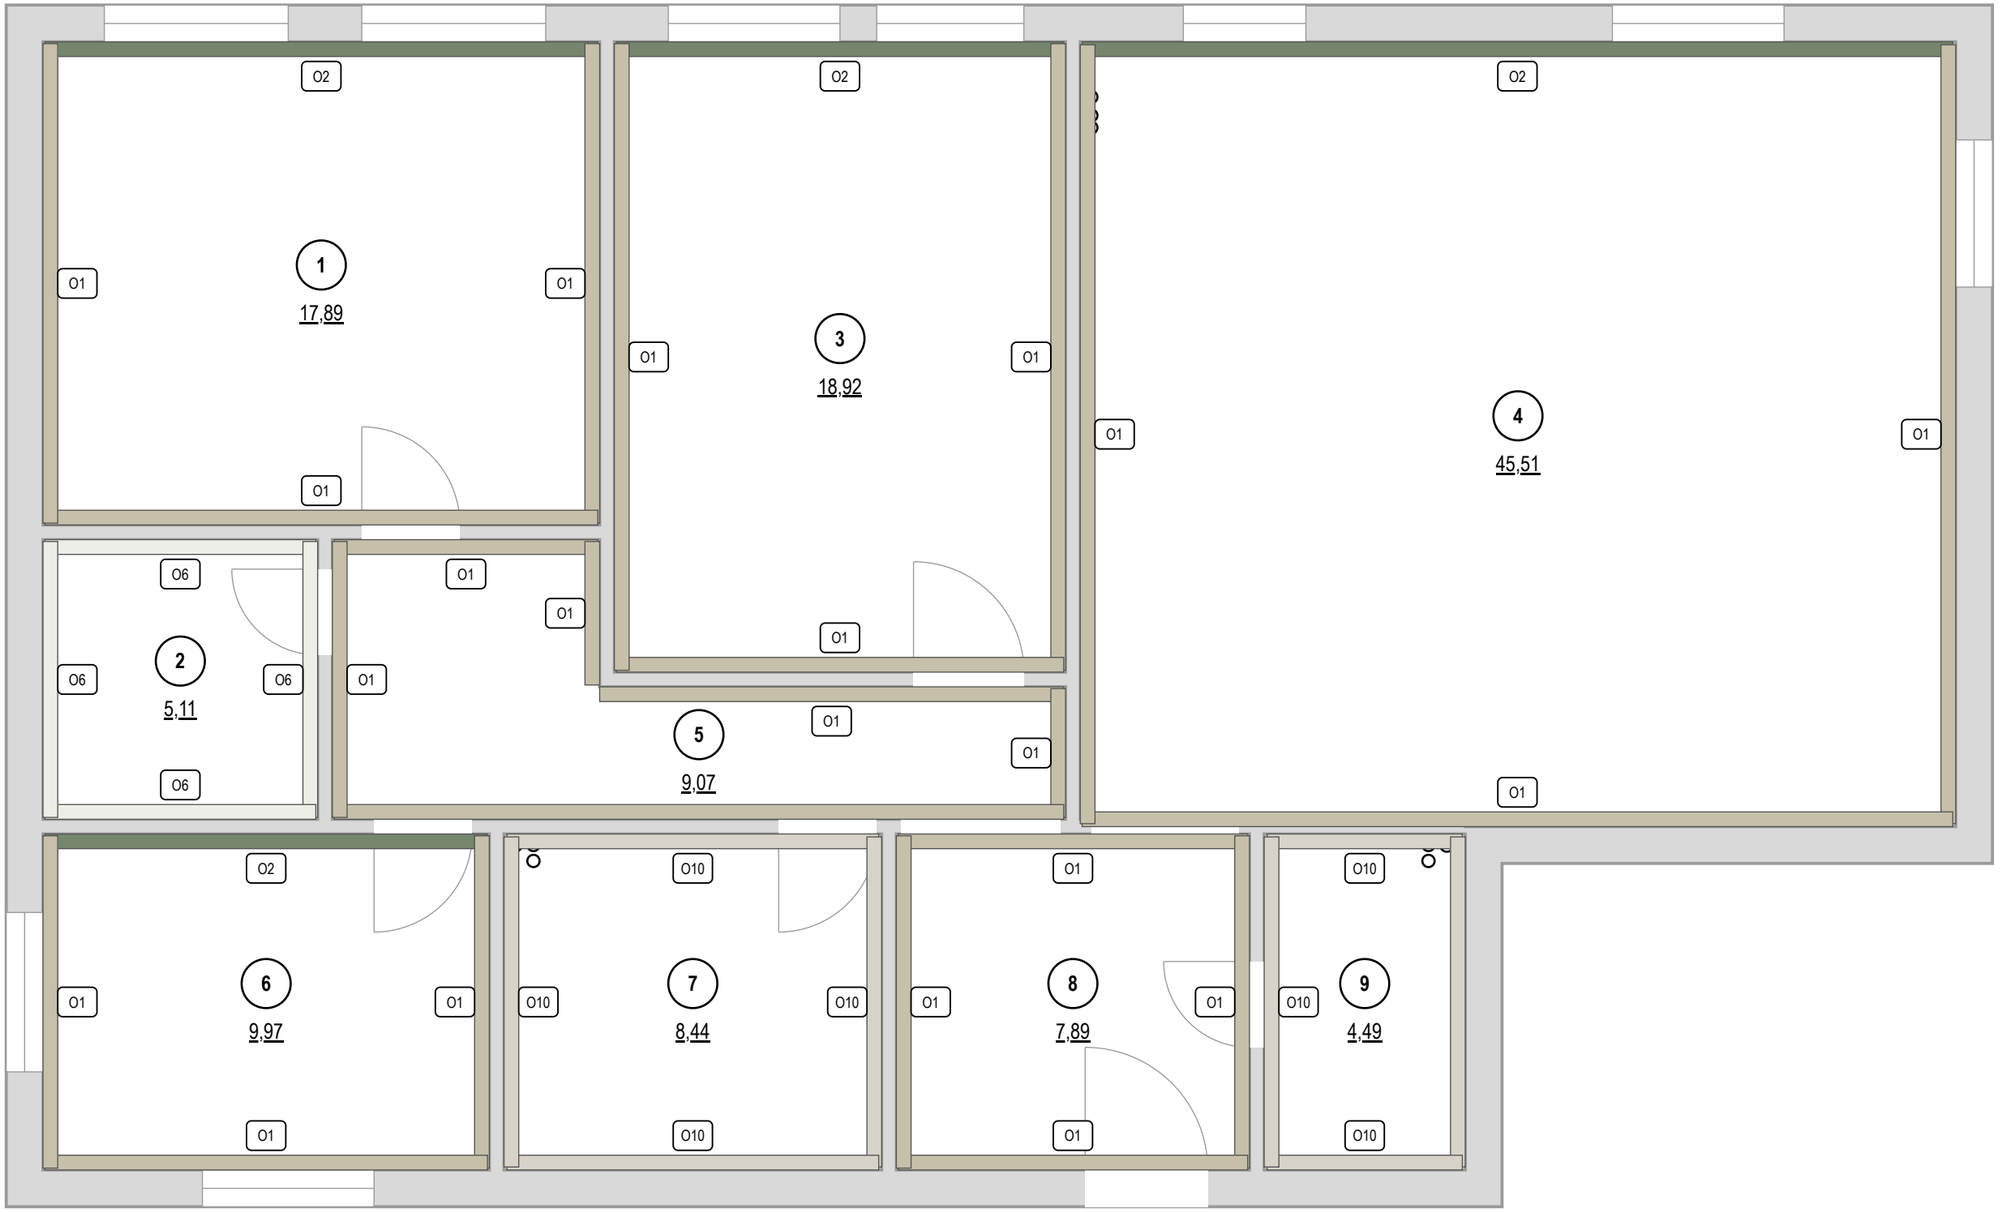

Покрытия стен

Марка	Покрытие	Помещение: S, м²	Итого, м²
O1	окраска Farrow & Ball · No. 15 «Bone — мягкий каменно-серый с зеленцой»	1: 31,6; 3: 35,6; 4: 48,7; 5: 33,0; 6: 20,1; 8: 21,2	190,2
O2	окраска Farrow & Ball · No. 34 «Calke Green — традиционный шалфей»	1: 7,4; 3: 5,7; 4: 14,3; 6: 8,1	35,5
O6	окраска Tikkurila · V503 «Winter»	2: 22,6	22,6
O10	облицовка плиткой Atlas Concorde · A8UZ «Marvel Travertine» 600×1200 мм	7: 25,8; 9: 19,1	45,0

Площади — нетто, по развёртками (за вычетом проёмов и фартука); высоты помещений — от чистого пола.

					Проект: Квартира с кабинетом
	Лист	№ док.	Подпись	Дата	
Дизайнер	Кырлан А.С.			21.10.26	Карта покрытий стен

Стадия	Лист	Листов
П	8	97

выпуск 18.10.2026 № 918b20bf25 · стр. 8 из 97

Колерная карта по помещениям

Помещение	Поверхность	Образец	Поз.	Система и код цвета	Производитель, линейка / материал, артикул	Блеск	Класс EN 13300	LRV	Площадь
1. Спальня 17,89 м²	стены		**К1**	Farrow & Ball No. 15	Farrow & Ball · Modern Emulsion	матовая	1	53	31,9 м²
	акцент А		**К2**	Farrow & Ball No. 34	Farrow & Ball · Modern Emulsion	матовая	1	22	7,5 м²
	потолок		**К3**	Tikkurila V503	Tikkurila · Anti-Reflex 2	глубокомат.	2	86	17,9 м²
	пол		**КМ1**	по образцу	Coswick · Вековые традиции				17,9 м²
	плинтус		**К4**	Farrow & Ball No. 15	МДФ · в цвет Farrow & Ball			53	16,2 м
2. Гардеробная-постирочная 5,11 м²	стены		**К5**	Tikkurila V503	Tikkurila · Harmony	матовая	1	86	22,9 м²
	потолок		**К3**	Tikkurila V503	Tikkurila · Anti-Reflex 2	глубокомат.	2	86	5,1 м²
	пол		**КМ1**	по образцу	Coswick · Вековые традиции				5,1 м²
	плинтус		**К6**	Tikkurila V503	МДФ · в цвет Tikkurila			86	8,3 м
3. Кабинет 18,92 м²	стены		**К1**	Farrow & Ball No. 15	Farrow & Ball · Modern Emulsion	матовая	1	53	35,8 м²
	акцент А		**К2**	Farrow & Ball No. 34	Farrow & Ball · Modern Emulsion	матовая	1	22	5,8 м²
	потолок		**К3**	Tikkurila V503	Tikkurila · Anti-Reflex 2	глубокомат.	2	86	18,9 м²
	пол		**КМ1**	по образцу	Coswick · Вековые традиции				18,9 м²
	плинтус		**К4**	Farrow & Ball No. 15	МДФ · в цвет Farrow & Ball			53	16,7 м
4. Кухня-гостиная 45,51 м²	стены		**К1**	Farrow & Ball No. 15	Farrow & Ball · Modern Emulsion	матовая	1	53	48,7 м²
	акцент А		**К2**	Farrow & Ball No. 34	Farrow & Ball · Modern Emulsion	матовая	1	22	15,6 м²
	потолок		**К3**	Tikkurila V503	Tikkurila · Anti-Reflex 2	глубокомат.	2	86	45,5 м²
	пол		**КМ1**	по образцу	Coswick · Вековые традиции				45,5 м²
	плинтус		**К4**	Farrow & Ball No. 15	МДФ · в цвет Farrow & Ball			53	25,9 м
	фартук		**КМ2**	по образцу	керамогранит · аналог по хар.				0,7 м²
5. Коридор 9,07 м²	стены		**К1**	Farrow & Ball No. 15	Farrow & Ball · Modern Emulsion	матовая	1	53	33,5 м²
	потолок		**К3**	Tikkurila V503	Tikkurila · Anti-Reflex 2	глубокомат.	2	86	9,1 м²
	пол		**КМ1**	по образцу	Coswick · Вековые традиции				9,1 м²
	плинтус		**К4**	Farrow & Ball No. 15	МДФ · в цвет Farrow & Ball			53	11,2 м
6. Детская 9,97 м²	стены		**К1**	Farrow & Ball No. 15	Farrow & Ball · Modern Emulsion	матовая	1	53	20,3 м²
	акцент А		**К2**	Farrow & Ball No. 34	Farrow & Ball · Modern Emulsion	матовая	1	22	8,1 м²
	потолок		**К3**	Tikkurila V503	Tikkurila · Anti-Reflex 2	глубокомат.	2	86	10,0 м²
	пол		**КМ1**	по образцу	Coswick · Вековые традиции				10,0 м²
	плинтус		**К7**	Farrow & Ball No. 15	Orac Decor · Contour (Luxxus)			53	12,0 м
7. Ванная 8,44 м²	стены		**К8**	Atlas Concorde A8UZ	Atlas Concorde · Marvel Travertine				26,3 м²
	потолок		**К9**	Tikkurila V503	Tikkurila · Luja 7	матовая	1	86	8,4 м²
	пол		**К8**	Atlas Concorde A8UZ	Atlas Concorde · Marvel Travertine				8,4 м²
8. Прихожая 7,89 м²	стены		**К1**	Farrow & Ball No. 15	Farrow & Ball · Modern Emulsion	матовая	1	53	21,5 м²
	потолок		**К3**	Tikkurila V503	Tikkurila · Anti-Reflex 2	глубокомат.	2	86	7,9 м²
	пол		**К8**	Atlas Concorde A8UZ	Atlas Concorde · Marvel Travertine				7,9 м²
	плинтус		**К4**	Farrow & Ball No. 15	МДФ · в цвет Farrow & Ball			53	7,0 м
9. Санузел гостевой 4,49 м²	стены		**К8**	Atlas Concorde A8UZ	Atlas Concorde · Marvel Travertine				19,6 м²
	потолок		**К9**	Tikkurila V503	Tikkurila · Luja 7	матовая	1	86	4,5 м²
	пол		**К8**	Atlas Concorde A8UZ	Atlas Concorde · Marvel Travertine				4,5 м²

Примечания

1. Цвет утверждается только по выкрасу на объекте: формат от А3 до 1000×1000 мм на загрунтованном ГКЛ, в 2 слоя (как на стене), не на белой шпаклёвке; смотреть днём и при свете проекта своего помещения, рядом с образцами пола и фасадов. Подпись на обороте: код, бренд и веер, дата.
2. Колеровка машинная в колеровочном центре бренда; каждый код — за один проход, одной партией на весь объём. Колеровщику передаётся только система и код утверждённого веера; плашки и HEX на листе — ориентир, печать не является эталоном цвета.
3. Класс мокрого истирания — EN 13300 (ISO 11998); блеск — по ГОСТ 31975 (ISO 2813), геометрия 60°. LRV — пересчёт координаты L каталога производителя ($Y = ((L^*+16)/116)^3$); «≈» — расчёт по HEX, справочно.
4. Площади поверхностей — тем же способом и с теми же цифрами, что в ведомости отделки (способ счёта — в общих указаниях); объём краски к заказу, фасовка и материалы КМ — в спецификации отделочных материалов.
5. Перечень выкрасов составлен по кодам колерной карты; к основному тону стен добавить на выкрас 2 соседних тона того же веера (светлее и темнее), статус отмечать в графе «Статус» при согласовании.

Схема палитры проекта


Стиль: Модерн (ар-нуво) 60% + Современный (контемпорари) 40% · схема: аналоговая

основной	основной	основной	второстепенный	второстепенный	акцентный	акцентный	акцентный
Farrow & Ball No. 15	**NCS S 2010-Y30R**	**Tikkurila V503**	**Farrow & Ball No. 34**	**Farrow & Ball No. 286**	**NCS S 5030-B10G**	**Farrow & Ball No. 66**	**NCS S 8010-Y30R**
Bone — мягкий каменно-серый с зеленцой LRV 53 стены 1,3,4,5,6,8; плинтус 1,3,4,5,6,8	Тёплый льняной беж LRV 60 текстиль/декор 1,3,4,6	Winter LRV 86 потолок 1,2,3,4,5,6,7,8,9; стены 2; плинтус 2; текстиль/декор 1,3,4,6	Calke Green — традиционный шалфей LRV 22 акцент 1,3,4,6; текстиль/декор 1,3,4,6	Peignoir — серо-розовый LRV 57 текстиль/декор 3,6	Павлиний сине-зелёный LRV 12 текстиль/декор 3,6	India Yellow — глубокая горчица LRV 36 текстиль/декор 3,4,6	Тёмно-коричневый LRV 3 в отделке не применён

План 60/30/10



Окраска, факт — по площади стен, акцентов, потолков

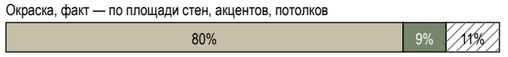

окрашено всего 424,8 м²; второстепенный тон несут мебель и текстиль

Текстиль и декор в цветах вне палитры проекта

NCS S 5020-G50Y Оливковый — пом. 1 (Т3)

Условные обозначения

- **К1** Farrow & Ball No. 15 · Bone — мягкий каменно-серый с зеленцой · Modern Emulsion · матовая · кл. 1
- **К2** Farrow & Ball No. 34 · Calke Green — традиционный шалфей · Modern Emulsion · матовая · кл. 1
- **К3** Tikkurila V503 · Winter · Anti-Reflex 2 · глубокомат. · кл. 2
- **К4** Farrow & Ball No. 15 · Bone — мягкий каменно-серый с зеленцой · МДФ
- **К5** Tikkurila V503 · Winter · Harmony · матовая · кл. 1
- **К6** Tikkurila V503 · Winter · МДФ
- **К7** Farrow & Ball No. 15 · Bone — мягкий каменно-серый с зеленцой · Contour (Luxxus)
- **К8** Atlas Concorde A8UZ · Marvel Travertine · Marvel Travertine
- **К9** Tikkurila V503 · Winter · Luja 7 · матовая · кл. 1
- **КМ1** инженерная доска · 1167-4250
- **КМ2** аналог: керамогранит под травертин, матовый, 1200×600×9 мм
- дерево (доска, паркет, ламинат) — рисунок досок
- керамогранит, плитка, камень — сетка швов по формату
- HEX не задан — цвет только по коду и вееру

К — позиция окраски (код + продукт + блеск), КМ — позиция материала, тон КМ — по описанию артикула, эталон — образец материала; ≈ LRV — расчёт по HEX, справочно

Перечень выкрасов на согласование

№	Код	Бренд / веер	Пом. / стена	Подложка	Формат	Статус
1	No. 15	Farrow & Ball	1, 3, 4, 5, 6, 8	ГКЛ, загрунтованный под эту краску; МДФ, загрунтованный под эмаль	600×1000; 300×600	к выполнению
2	No. 34	Farrow & Ball	1 А, 3 А, 4 А, 6 А	ГКЛ, загрунтованный под эту краску	600×1000	к выполнению
3	V503	Tikkurila	1, 2, 3, 4, 5, 6, 7, 8, 9	ГКЛ, загрунтованный под эту краску; МДФ, загрунтованный под эмаль	600×1000; 300×600	к выполнению

					Проект: Квартира с кабинетом
	Лист	№ док.	Подпись	Дата	
Дизайнер	Кырлан А.С.			21.10.26	Колерная карта

Стадия	Лист	Листов
П	9	97

Правка к этому листу

ОБ_01 ТВ на стене 1600×350 h 450
М_02 Тумба прикроватная 500×400 h 550
М_13 Стеллаж-библиотека с арками 2000×350 h 2400
М_08 Шкаф распашной с арочными фасадами 2550×600 h 2400
М_17 Модуль с ящиками 600×600 h 900
М_15 Модуль под мойку у окна 800×600 h 900
М_16 Посудомоечная машина встроенная 600×600 h 900
М_20 Банкетка-диван вдоль окон 3200×600 h 850
М_14 Колонна с холодильником 600×650 h 2100
М_18 Колонна 600×600 h 2100
М_03 Тумба прикроватная 500×400 h 550
М_01 Кровать с высоким 1700×2150 h 450
М_09 Рабочий стол 1000×1700 h 750
М_04 Туалетный столик с овальным 1200×450 h 780
М_05 Кресло-ракушка 750×750 h 800
М_10 Кресло рабочее 650×650 h 900
М_11 Диван 2150 с мягкими 2150×950 h 800
М_12
ОБ_02 ТВ на стене 1500×350 h 450
кухня
М_30 Стул обеденный к столу М_21 ×6
столовая
гостиная
М_21 Стол обеденный овальный 1800×1000 h 750
М_19 Остров с варочной панелью 900×1400 h 900
М_23 Столик журнальный органической формы 1100×700 h 380
М_24 Шкаф встроенный 3500×500 h 2400
ОБ_03 ТВ-стена с биокамином 1800×400 h 500
М_22 Диван угловой модульный с 2700×1000 h 800
М_06
М_07
М_27 Подвесное кресло-кокон 900×900 h 1100
М_25 Шкаф с арочной нишей 1400×600 h 2400
М_26 Кровать с мягким 900×2000 h 450
М_28 Шкаф-купе с зеркальными арками 2000×600 h 2600
М_29 Пуф и вешалка 700×400 h 450

1 17,89 · 2 5,11 · 3 18,92 · 4 45,51 · 5 9,07 · 6 9,97 · 7 8,44 · 8 7,89 · 9 4,49

Экспликация помещений

лист обмерного плана · на плане — номера в марках

Ведомость мебели и оборудования

33 позиц. (38 шт.) — расшифровка марок:
полностью на листе 11 «Спецификация мебели и оборудования»
марка, наименование, Ш×Г×В, материал, модель,
допуск замены. Марки на плане — по ней.

Примечания

1. Размеры — в мм от чистовых поверхностей стен; размеры мебели уточнить после отделочных работ; общие указания — лист 2.
2. Стулья обеденной группы (М_30 — 6 шт.) показаны в рабочем положении, задвинутыми под столешницу на 150 мм.

					Проект: Квартира с кабинетом
	Лист	№ док.	Подпись	Дата	План размещения мебели и оборудования
Дизайнер	Кырлан А.С.			21.10.26	

Стадия	Лист	Листов
П	10	97

выпуск 18.10.2026 № 918b20bf25 · стр. 10 из 97

Правка к этому листу

Поз.	Наименование и техническая характеристика	Тип, марка, обозначение документа, опросного листа	Код продукции	Поставщик	Ед. измерения	Кол.	Масса 1 ед., кг	Примечание
	Мебель встроенная и корпусная (изготовление по чертежам мебельщика)							
M_06	Система хранения: штанги, полки, ящики; каркас и полки — ЛДСП, декор «дуб натуральный»; Ш×Г×В 2200×600×2400 мм			изготовление на заказ	шт.	1		пом. 2; крепление к стене
M_07	Шкаф с выдвижной гладильной доской и полками; каркас и полки — ЛДСП, декор «дуб натуральный»; Ш×Г×В 1500×550×2400 мм			изготовление на заказ	шт.	1		пом. 2; крепление к стене
M_08	Шкаф распашной с арочными фасадами; корпус ЛДСП, фасады — матовая эмаль в цвет стен (Farrow & Ball No. 15); Ш×Г×В 2550×600×2400 мм			изготовление на заказ	шт.	1		пом. 3
M_14	Колонна с холодильником; корпус ЛДСП, фасады — матовая эмаль в тон стен; Ш×Г×В 600×650×2100 мм			изготовление на заказ	шт.	1		пом. 4
M_15	Модуль под мойку у окна; корпус ЛДСП, фасады — матовая эмаль в тон стен; Ш×Г×В 800×600×900 мм			изготовление на заказ	шт.	1		пом. 4
M_16	Посудомоечная машина встроенная; корпус ЛДСП, фасады — матовая эмаль в тон стен; Ш×Г×В 600×600×900 мм			изготовление на заказ	шт.	1		пом. 4
M_17	Модуль с ящиками; корпус ЛДСП, фасады — матовая эмаль в тон стен; Ш×Г×В 600×600×900 мм			изготовление на заказ	шт.	1		пом. 4
M_18	Колонна: духовой шкаф и СВЧ; корпус ЛДСП, фасады — матовая эмаль в тон стен; Ш×Г×В 600×600×2100 мм			изготовление на заказ	шт.	1		пом. 4
M_19	Остров 900×1400 с варочной панелью, столешница — травертин; корпус ЛДСП, фасады — матовая эмаль в тон стен; Ш×Г×В 900×1400×900 мм			изготовление на заказ	шт.	1		пом. 4
M_24	Шкаф встроенный, фасады с округлыми торцами; корпус ЛДСП, фасады — матовая эмаль в цвет стен (Farrow & Ball No. 15); Ш×Г×В 3500×500×2400 мм			изготовление на заказ	шт.	1		пом. 4
M_25	Шкаф с арочной нишей; корпус ЛДСП, фасады — матовая эмаль в цвет стен (Farrow & Ball No. 15); Ш×Г×В 1400×600×2400 мм			изготовление на заказ	шт.	1		пом. 6; крепление к стене
M_28	Шкаф-купе с зеркальными арками; корпус ЛДСП, фасады — матовая эмаль в цвет стен (Farrow & Ball No. 15); Ш×Г×В 2000×600×2600 мм			изготовление на заказ	шт.	1		пом. 8
	Мебель покупная							
M_01	Кровать 1700×2150 с высоким округлым изголовьем, бархат; мягкое изголовье, обивка — ткань, цвет Farrow & Ball No. 34; Ш×Г×В 1700×2150×450 мм			аналог по характеристикам	шт.	1		пом. 1; замена ≤ габарита
M_02, M_03	Тумба прикроватная, морёный дуб, латунные ручки; шпон, дуб натуральный, матовое масло; Ш×Г×В 500×400×550 мм			аналог по характеристикам	шт.	2		пом. 1; замена ≤ габарита
M_04	Туалетный столик с овальным зеркалом в латунной раме; шпон, дуб натуральный, матовое масло; Ш×Г×В 1200×450×780 мм			аналог по характеристикам	шт.	1		пом. 1; замена ≤ габарита
M_05	Кресло-ракушка, бархат павлиньего цвета; обивка — ткань, цвет Farrow & Ball No. 34; Ш×Г×В 750×750×800 мм			аналог по характеристикам	шт.	1		пом. 1; замена ≤ габарита
ОБ_01	ТВ на стене, тумба подвесная с волнистым фасадом; шпон, дуб натуральный, матовое масло; Ш×Г×В 1600×350×450 мм			аналог по характеристикам	шт.	1		пом. 1; замена ≤ габарита
M_09	Рабочий стол 1700×1000, морёный дуб, округлые углы; шпон, дуб натуральный, матовое масло; Ш×Г×В 1000×1700×750 мм			аналог по характеристикам	шт.	1		пом. 3; замена ≤ габарита
M_10	Кресло рабочее, кожа карамельного цвета; обивка — ткань, цвет Farrow & Ball No. 34; Ш×Г×В 650×650×900 мм			аналог по характеристикам	шт.	1		пом. 3; замена ≤ габарита
M_11	Диван 2150 с мягкими округлыми подлокотниками; обивка — ткань, цвет Farrow & Ball No. 34; Ш×Г×В 2150×950×800 мм			аналог по характеристикам	шт.	1		пом. 3; замена ≤ габарита
M_12	Столик кофейный круглый, травертин; шпон, дуб натуральный, матовое масло; Ш×Г×В 800×800×420 мм			аналог по характеристикам	шт.	1		пом. 3; замена ≤ габарита
M_13	Стеллаж-библиотека с арками; шпон, дуб натуральный, матовое масло; Ш×Г×В 2000×350×2400 мм			аналог по характеристикам	шт.	1		пом. 3; замена ≤ габарита
ОБ_02	ТВ на стене, тумба подвесная; шпон, дуб натуральный, матовое масло; Ш×Г×В 1500×350×450 мм			аналог по характеристикам	шт.	1		пом. 3; замена ≤ габарита
M_20	Банкетка-диван вдоль окон, бархат; Ш×Г×В 3200×600×850 мм			аналог по характеристикам	шт.	1		пом. 4; замена ≤ габарита
M_21	Стол обеденный овальный 1800×1000, морёный дуб; шпон, дуб натуральный, матовое масло; Ш×Г×В 1800×1000×750 мм			аналог по характеристикам	шт.	1		пом. 4; замена ≤ габарита

Примечания

1. Позиции мебели совпадают с марками на плане расстановки; размеры Ш×Г×В — Ш вдоль стены, Г от стены.
2. Встроенная и корпусная мебель изготавливается по чертежам мебельщика после контрольного обмера; графы «Тип, марка» и «Код продукции» для неё не заполняются (ГОСТ 21.110-2013).
3. Покупные изделия — аналог по характеристикам: заменять только на изделия не больше указанного габарита и того же материала и цвета.
4. Материал и цвет, не указанные в данных изделия, приняты по концепции: тон дерева — по полу, обивка — по вторичному цвету палитры; образцы согласовать до заказа.
5. Масса 1 ед. для изделий до 25 кг не указывается. Техника — по монтажным схемам изготовителя; выводы — по листам ЭОМ и ВК.

					Проект: Квартира с кабинетом
	Лист	№ док.	Подпись	Дата	Спецификация мебели и оборудования
Дизайнер	Кырлан А.С.			21.10.26	

Стадия	Лист	Листов
П	11	97

Правка к этому листу

Поз.	Наименование и техническая характеристика	Тип, марка, обозначение документа, опросного листа	Код продукции	Поставщик	Ед. измерения	Кол.	Масса 1 ед., кг	Примечание
M_22	Диван угловой модульный с округлыми формами, бархат павлиньего цвета; обивка — ткань, цвет Farrow & Ball No. 34; Ш×Г×В 2700×1000×800 мм			аналог по характеристикам	шт.	1		пом. 4; замена ≤ габарита
M_23	Столик журнальный органической формы, травертин; шпон, дуб натуральный, матовое масло; Ш×Г×В 1100×700×380 мм			аналог по характеристикам	шт.	1		пом. 4; замена ≤ габарита
M_30	Стул обеденный к столу M_21; обивка — ткань, цвет Farrow & Ball No. 34; каркас — дуб натуральный; Ш×Г×В 450×500×820 мм			аналог по характеристикам	шт.	6		пом. 4; замена ≤ габарита
ОБ_03	ТВ-стена с биокамином, панели с волнистым рельефом; шпон, дуб натуральный, матовое масло; Ш×Г×В 1800×400×500 мм			аналог по характеристикам	шт.	1		пом. 4; замена ≤ габарита
M_26	Кровать 900×2000 с мягким изголовьем-облаком; мягкое изголовье, обивка — ткань, цвет Farrow & Ball No. 34; Ш×Г×В 900×2000×450 мм			аналог по характеристикам	шт.	1		пом. 6; замена ≤ габарита
M_27	Подвесное кресло-кокон; обивка — ткань, цвет Farrow & Ball No. 34; Ш×Г×В 900×900×1100 мм			аналог по характеристикам	шт.	1		пом. 6; замена ≤ габарита
M_29	Пуф и вешалка; Ш×Г×В 700×400×450 мм			аналог по характеристикам	шт.	1		пом. 8; замена ≤ габарита
	Техника встраиваемая и бытовая, светильники под розетки							
	Холодильник встраиваемый, в модуле M_14			аналог по характеристикам	шт.	1		пом. 4; по схеме изготовителя
	Посудомоечная машина встраиваемая, в модуле M_16; ниша 600 мм			аналог по характеристикам	шт.	1		пом. 4; по схеме изготовителя
	Духовой шкаф встраиваемый, в модуле M_18			аналог по характеристикам	шт.	1		пом. 4; по схеме изготовителя
	СВЧ-печь встраиваемая, в модуле M_18			аналог по характеристикам	шт.	1		пом. 4; по схеме изготовителя
	Варочная панель встраиваемая, электрическая, в модуле M_19			аналог по характеристикам	шт.	1		пом. 4; по схеме изготовителя
	Вытяжка, у M_24			аналог по характеристикам	шт.	1		пом. 4; вывод ЭВЗ (ЭОМ)
	Стиральная машина, место по листу ВК (ОБ_04); Ш×Г 600×600 мм			аналог по характеристикам	шт.	1		пом. 7; по схеме изготовителя
	Торшер, у поз. ОБ_01; абажур — ткань или опаловое стекло; лампа 2700 K			аналог по характеристикам	шт.	1		пом. 1; розетка Р5 (ЭОМ)
	Торшер, у поз. M_15; абажур — ткань или опаловое стекло; лампа 2700 K			аналог по характеристикам	шт.	1		пом. 4; розетка Р21 (ЭОМ)
	Текстиль							
T1	Портьеры-волна; лён 100 %; цвет NCS S 2010-Y30R; карниз 2500 мм, высота 2610 мм, сборка 2			аналог по характеристикам	шт.	2		пом. 1
T2	Тюль; полиэстер 100 %; цвет Tikkurila V503; карниз 2500 мм, высота 2610 мм, сборка 2,5			аналог по характеристикам	шт.	1		пом. 1
T3	Ковёр под кроватью; шерсть 80 %, хлопок 20 %; цвет NCS S 5020-G50Y; 2800×1850 мм			аналог по характеристикам	шт.	1		пом. 1; с подложкой
T4	Подушки декоративные на кровать; лён 100 %; цвет NCS S 2010-Y30R			аналог по характеристикам	шт.	3		пом. 1
T5	Подушки на кровать, акцент; хлопковый бархат 100 %; цвет Farrow & Ball No. 34			аналог по характеристикам	шт.	2		пом. 1
T6	Плед на кровать; шерсть мериноса 100 %; цвет Farrow & Ball No. 34			аналог по характеристикам	шт.	1		пом. 1
T7	Портьеры-волна; лён 100 %; цвет NCS S 2010-Y30R; карниз 1820 мм, высота 2610 мм, сборка 2			аналог по характеристикам	шт.	2		пом. 3
T8	Тюль; полиэстер 100 %; цвет Tikkurila V503; карниз 1820 мм, высота 2610 мм, сборка 2,5			аналог по характеристикам	шт.	1		пом. 3
T9	Ковёр под кроватью; шерсть 100 %; цвет Farrow & Ball No. 66; 2500×1800 мм			аналог по характеристикам	шт.	1		пом. 3; с подложкой
T10	Подушки декоративные на кровать; букле (шерсть 60 %, полиэстер 40 %); цвет Farrow & Ball No. 286			аналог по характеристикам	шт.	3		пом. 3

						Проект: Квартира с кабинетом		
	Лист	№ док.	Подпись	Дата				
Дизайнер	Кырлан А.С.			21.10.26	Спецификация мебели и оборудования (продолжение)	Стадия	Лист	Листов
						П	12	97

Правка к этому листу

Поз.	Наименование и техническая характеристика	Тип, марка, обозначение документа, опросного листа	Код продукции	Поставщик	Ед. измерения	Кол.	Масса 1 ед., кг	Примечание
Т11	Подушки на кровать, акцент; хлопковый бархат 100 %; цвет NCS S 5030-B10G			аналог по характеристикам	шт.	2		пом. 3
Т12	Плед на кровать; шерсть мериноса 100 %; цвет Farrow & Ball No. 34			аналог по характеристикам	шт.	1		пом. 3
Т13	Портьеры-волна (гостиная); лён 70 %, вискоза 30 %; цвет NCS S 2010-Y30R; карниз 2250 мм, высота 2610 мм, сборка 2			аналог по характеристикам	шт.	2		пом. 4
Т14	Тюль (гостиная); полиэстер 100 %; цвет Tikkurila V503; карниз 2250 мм, высота 2610 мм, сборка 2,5			аналог по характеристикам	шт.	1		пом. 4
Т15	Римская штора (кухня); лён 100 %; цвет Farrow & Ball No. 66; карниз 1400 мм, высота 1620 мм			аналог по характеристикам	шт.	1		пом. 4
Т16	Ковёр в зоне отдыха; шерсть 100 %; цвет Farrow & Ball No. 66; 3000×1150 мм			аналог по характеристикам	шт.	1		пом. 4; с подложкой
Т17	Подушки на диван; букле (шерсть 60 %, полиэстер 40 %); цвет NCS S 2010-Y30R			аналог по характеристикам	шт.	3		пом. 4
Т18	Подушки на диван, акцент; хлопковый бархат 100 %; цвет Farrow & Ball No. 34			аналог по характеристикам	шт.	2		пом. 4
Т19	Плед на диван; альпака 50 %, шерсть 50 %; цвет Farrow & Ball No. 66			аналог по характеристикам	шт.	1		пом. 4
Т20	Портьеры-волна; лён 100 %; цвет NCS S 2010-Y30R; карниз 1820 мм, высота 2610 мм, сборка 2			аналог по характеристикам	шт.	2		пом. 6
Т21	Тюль; полиэстер 100 %; цвет Tikkurila V503; карниз 1820 мм, высота 2610 мм, сборка 2,5			аналог по характеристикам	шт.	1		пом. 6
Т22	Ковёр под кроватью; шерсть 100 %; цвет Farrow & Ball No. 66; 2500×1800 мм			аналог по характеристикам	шт.	1		пом. 6; с подложкой
Т23	Подушки декоративные на кровать; букле (шерсть 60 %, полиэстер 40 %); цвет Farrow & Ball No. 286			аналог по характеристикам	шт.	3		пом. 6
Т24	Подушки на кровать, акцент; хлопковый бархат 100 %; цвет NCS S 5030-B10G			аналог по характеристикам	шт.	2		пом. 6
Т25	Плед на кровать; шерсть мериноса 100 %; цвет Farrow & Ball No. 34			аналог по характеристикам	шт.	1		пом. 6
	Декор							
ДК1	Картина над кроватью: абстракция, холст, тонкая рама из дуба; 1200×700 мм; низ на 1300 мм от пола			аналог по характеристикам	шт.	1	4	пом. 1; крепление к стене
ДК3	Картина над диваном: графика в паспарту, рама — дуб; 1400×700 мм; низ на 1000 мм от пола			аналог по характеристикам	шт.	1	4	пом. 3; крепление к стене
ДК4	Зеркало в рост в тонкой чёрной раме; рама — чёрный матовый; 600×1600 мм; низ на 300 мм от пола			аналог по характеристикам	шт.	1	12	пом. 3; крепление: анкер для пустотелых оснований, 4 шт.
ДК6	Картина: крупная абстракция в тёплой гамме, холст на подрамнике; 1200×900 мм; центр на 1550 мм от пола			аналог по характеристикам	шт.	1	6	пом. 4; крепление: анкер, 2 шт.
ДК7	Растение в кашпо; 450×450 мм			аналог по характеристикам	шт.	1		пом. 4
ДК8	Ваза керамическая с ветками на обеденном столе; 200×350 мм; на М5			аналог по характеристикам	шт.	1		пом. 4
ДК2	Картина над кроватью: графика в паспарту, рама — дуб; 600×700 мм; низ на 1100 мм от пола			аналог по характеристикам	шт.	1	4	пом. 6; крепление к стене
ДК5	Зеркало в рост в тонкой чёрной раме; рама — чёрный матовый; 600×1600 мм; низ на 300 мм от пола			аналог по характеристикам	шт.	1	12	пом. 6; крепление: анкер для пустотелых оснований, 4 шт.
ДК9	Зеркало; рама — чёрный матовый; 800×1800 мм; низ на 550 мм от пола			аналог по характеристикам	шт.	1	18	пом. 8; крепление: анкер, 4 шт.

					Проект: Квартира с кабинетом	
	Лист	№ док.	Подпись	Дата	Спецификация мебели и оборудования (продолжение)	Стадия / Лист / Листов
Дизайнер	Кырлан А.С.			21.10.26		П / 13 / 97

Правка к этому листу

Ведомость изделий

Марка	Наименование	Пом.	Ш×Г×В, мм	Корпус	Фасад	Кромка, мм скр./вид.	Кол.
M_06	Система хранения	2	2200×600×2400	ЛДСП 16	без фасадов; ящики — МДФ 18, эмаль матовая	0,4 / 2	1
M_07	Система хранения	2	1500×550×2400	ЛДСП 16	без фасадов; ящики — МДФ 18, эмаль матовая	0,4 / 2	1
M_08	Шкаф распашной	3	2550×600×2400	ЛДСП 16	МДФ 18, эмаль матовая	0,4 / 2	1
M_24	Шкаф распашной	4	3500×500×2400	ЛДСП 16	МДФ 18, эмаль матовая	0,4 / 2	1
M_25	Шкаф распашной	6	1400×600×2400	ЛДСП 16	МДФ 18, эмаль матовая	0,4 / 2	1
M_28	Шкаф-купе	8	2000×600×2600	ЛДСП 16	рифлёные панели МДФ в алюминиевом профиле	0,4 / 2	1
M_15	Модуль нижний: мойка	4	800×600×900	ЛДСП 16	МДФ 18, эмаль матовая	0,4 / 2	1
M_16	Модуль нижний: ПММ	4	600×600×900	ЛДСП 16	МДФ 18, эмаль матовая	0,4 / 2	1
M_17	Модуль нижний: ящики	4	600×600×900	ЛДСП 16	МДФ 18, эмаль матовая	0,4 / 2	1
M_18	Пенал: полки	4	600×600×2100	ЛДСП 16	МДФ 18, эмаль матовая	0,4 / 2	1
M_14	Пенал: холодильник встр.	4	600×650×2100	ЛДСП 16	МДФ 18, эмаль матовая	0,4 / 2	1

Ведомость встраиваемой техники

Поз.	Прибор	Ниша, вырез, мм	Вентиляция	Питание	Схема
M_15	Мойка врезная / подстольная с сифоном	вырез по шаблону, ориентир 700 × 480		смеситель — выводы ВК	по модели
M_16	Посудомоечная машина встраиваемая, 60 см	ниша 600 × 862 (от пола до низа столешницы)	зазор в цоколе, по схеме	розетка в соседнем модуле	по модели
M_14	Холодильник встраиваемый, ниша 1780	ниша 1780 × 560 × 550	решётка в цоколе, канал за корпусом, выход сверху	розетка над нишей или в соседнем модуле	по модели

Ведомость фурнитуры

№	Фурнитура	Тип, размер	Изделия	Кол.
1	Полкодержатель с фиксацией	ø5 мм	M_06, M_07, M_08, M_24, M_25, M_28, M_18, M_14	208
2	Штанга овальная 30×15, L = 712	+ 2 держателя	M_06	3
3	Опора регулируемая с цоколем на клипсах	ход 20 мм	M_06, M_07, M_08, M_24, M_25, M_28	50
4	Анкер по основанию стены	по таблице крепежа	M_06, M_07, M_08, M_24, M_25, M_28	43
5	Уголок крепления к стене от опрокидывания	стальной	M_06, M_07, M_08, M_24, M_25, M_28, M_18, M_14	16
6	Штанга овальная 30×15, L = 726	+ 2 держателя	M_07	1
7	Петля накладная 110° с доводчиком	чашка 35 мм	M_08, M_24, M_25, M_15, M_18, M_14	106
8	Штанга овальная 30×15, L = 996	+ 2 держателя	M_08	2
9	Штанга овальная 30×15, L = 486	+ 2 держателя	M_08	1
10	Штанга выдвижная торцевая	L по глубине	M_24	2
11	Штанга овальная 30×15, L = 909	+ 2 держателя	M_25	1
12	Система дверей купе: профиль, направляющие, ролики	на 3 двери	M_28	1
13	Ручка-профиль вертикальная	в цвет профиля	M_28	3
14	Штанга овальная 30×15, L = 653	+ 2 держателя	M_28	3
15	Полка для обуви выдвижная наклонная	ширина 630	M_28	2
16	Полка для обуви выдвижная наклонная	ширина 653	M_28	1
17	Ручка-профиль	латунь матовая	M_15, M_16, M_17, M_18, M_14	11
18	Опора кухонная регулируемая 100–120 мм	+ клипса цоколя	M_15, M_16, M_17, M_18, M_14	22
19	Комплект навески фасада ПММ	из поставки машины	M_16	1
20	Направляющие полного выдвижения с доводчиком NL 500	пара	M_17	3

Примечания

1. Модели техники выбирает заказчик до изготовления мебели; ниши, вырезы и вентиляция — по монтажной схеме выбранной модели (условие гарантии), её номер вносится в ведомость.
2. Количество фурнитуры — по чертежам изделий; запас крепежа 5 %. Аналоги — по характеристикам (доводчик, нагрузка, ход).
3. Цвет корпусов, фасадов и профилей — по колерной карте проекта.


					Проект: Квартира с кабинетом
	Лист	№ док.	Подпись	Дата	Ведомости изделий, техники и фурнитуры
Дизайнер	Кырлан А.С.			21.10.26	

Стадия	Лист	Листов
П	14	97


выпуск 18.10.2026 № 918b20bf25 · стр. 14 из 97

Правка к этому листу


Фрагмент 1. Ванная (пом. 7)

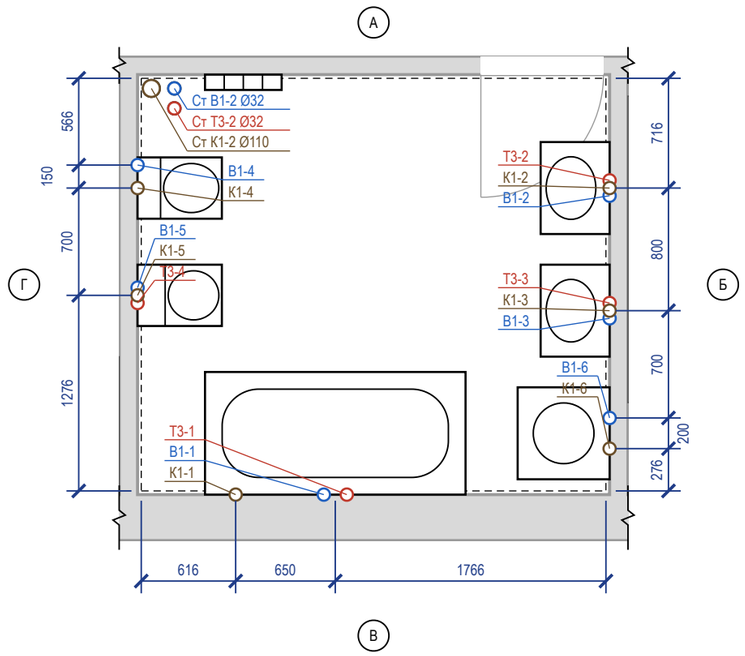

Фрагмент 2. Санузел гостевой (пом. 9)

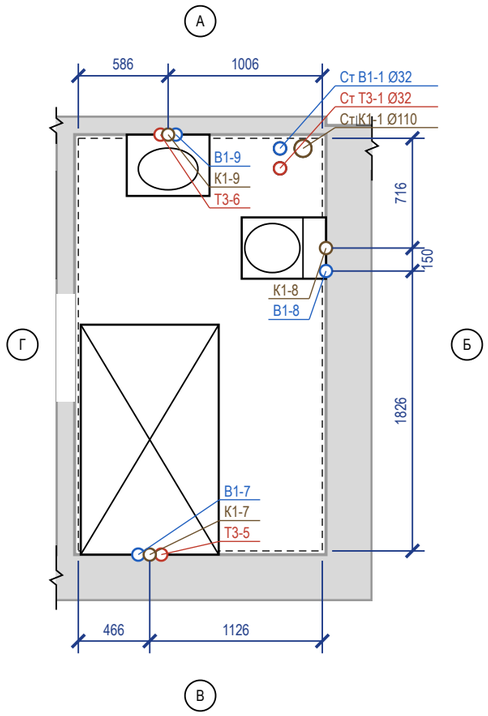

Фрагмент 3. Кухня-гостиная (пом. 4)

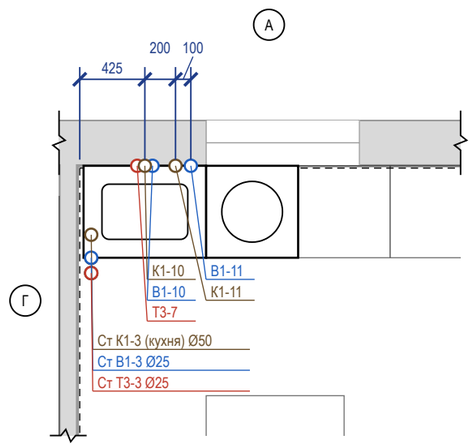

Примечания

1. Привязки выводов даны от чистовых поверхностей стен (облицовка на сторону: ванная — 24 мм (штукатурка 10 + клей 5 + плитка 9); санузел гостевой 24 мм (штукатурка 10 + клей 5 + плитка 9); кухня-гостиная — 24 мм (фартук: штукатурка 10 + клей 5 + плитка 9)); эти же грани — на развёртках и в раскладке плитки. Высоты — от чистого пола помещения.
2. До черновой разводки сверить по паспорту выбранного прибора (смеситель, инсталляция, сифон).
3. Горячая вода (Т3) — слева от холодной (В1), если смотреть на прибор. Допуск установки выводов: ±5 мм в группе, ±20 мм у отдельно стоящих.
4. Расчёт систем водоснабжения и канализации и подбор оборудования выполняет проектная организация; лист задаёт места и высоты выводов.
5. Посудомоечная машина П12: кран и слив — отдельными выводами в шкафу мойки (не за машиной), до машины ≤ 1500 мм.
6. Прибор П11 мойка кухонная, П12 посудомоечная машина взят из расстановки мебели (по шкафу с мойкой).
7. Стояки в коробах/шахтах не замоноличивать; стояк К1 в коробе — звукоизоляция стояка в коробе без жёсткого контакта с трубой; к арматуре и ревизиям — люк не меньше 300×400.

Ведомость привязок выводов

Код	Прибор	Ø	Н, мм	Привязка от чист. стен, мм	Прим.
В1-1	С_01 ванна	½"	200	ст. В: 1191 от Г	межос. 150
Т3-1	С_01 ванна	½"	200	ст. В: 1341 от Г	межос. 150
К1-1	С_01 ванна	Ø50	50	ст. В: 616 от Г	
В1-2	С_02 умывальник	½"	550	ст. Б: 766 от А	межос. 100
Т3-2	С_02 умывальник	½"	550	ст. Б: 666 от А	межос. 100
К1-2	С_02 умывальник	Ø50	500	ст. Б: 716 от А	
В1-3	С_03 умывальник	½"	550	ст. Б: 1126 от В	межос. 100
Т3-3	С_03 умывальник	½"	550	ст. Б: 1226 от В	межос. 100
К1-3	С_03 умывальник	Ø50	500	ст. Б: 1176 от В	
В1-4	С_04 унитаз подвесной	½"	1000	ст. Г: 566 от А	в раме инсталляции
К1-4	С_04 унитаз подвесной	Ø110	220	ст. Г: 716 от А	
В1-5	С_05 биде	½"	200	ст. Г: 1326 от В	межос. 100
Т3-4	С_05 биде	½"	200	ст. Г: 1226 от В	межос. 100
К1-5	С_05 биде	Ø50	200	ст. Г: 1276 от В	
В1-6	ОБ_04 стиральная машина	½"	800	ст. Б: 476 от В	кран машины
К1-6	ОБ_04 стиральная машина	Ø50	600	ст. Б: 276 от В	
В1-7	С_07 душ	½"	1000	ст. В: 391 от Г	межос. 150
Т3-5	С_07 душ	½"	1000	ст. В: 541 от Г	межос. 150
К1-7	С_07 душ	Ø50	0	ст. В: 466 от Г	сифон поддона
В1-8	С_08 унитаз подвесной	½"	1000	ст. Б: 866 от А	в раме инсталляции
К1-8	С_08 унитаз подвесной	Ø110	220	ст. Б: 716 от А	
В1-9	С_09 умывальник	½"	550	ст. А: 636 от Г	межос. 100
Т3-6	С_09 умывальник	½"	550	ст. А: 536 от Г	межос. 100
К1-9	С_09 умывальник	Ø50	500	ст. А: 586 от Г	
В1-10	П11 мойка кухонная	½"	600	ст. А: 475 от Г	межос. 100
Т3-7	П11 мойка кухонная	½"	600	ст. А: 375 от Г	межос. 100
К1-10	П11 мойка кухонная	Ø50	400	ст. А: 425 от Г	
В1-11	П12 посудомоечная машина	½"	550	ст. А: 725 от Г	кран ПММ в шкафу мойки
К1-11	П12 посудомоечная машина	Ø40	550	ст. А: 625 от Г	слив ПММ в шкафу мойки

Условные обозначения

- вывод В1 (код — в ведомости привязок)
- вывод Т3 (код — в ведомости привязок)
- вывод К1 (код — в ведомости привязок)
- сантехприбор по расстановке (габарит модели)
- чистовая поверхность стены (от неё привязки)
- стояк «Ст К1-N / Ст В1-N» (ГОСТ 21.601), Ø мм
- линия обрыва (граница фрагмента)
- А — обозначение стены А–Г (как на развёртках)


					Проект: Квартира с кабинетом
	Лист	№ док.	Подпись	Дата	План выводов сантехники
Дизайнер	Кырлан А.С.			21.10.26	

Стадия	Лист	Листов
П	15	97


выпуск 18.10.2026 № 918b20bf25 · стр. 15 из 97

Правка к этому листу


План квартиры (М 1:400)

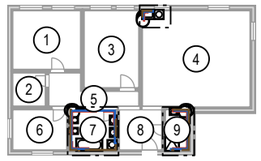


Фр. 1. Ванная (М 1:40)

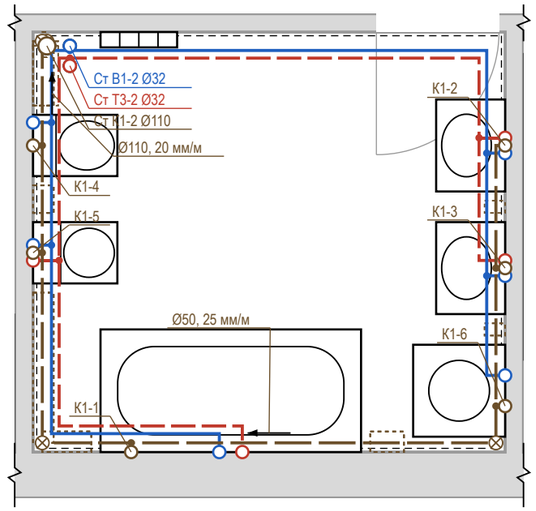

Фр. 2. Санузел гостевой (М 1:40)

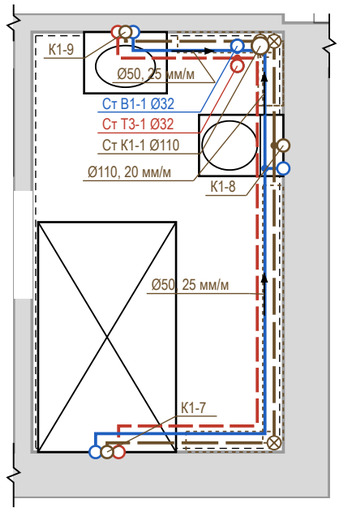

Фр. 3. Кухня-гостиная (М 1:40)

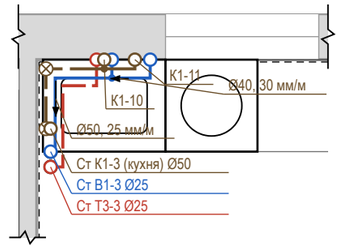

Условные обозначения


- В1 — водопровод хозяйственно-питьевой (ХВС), PP-R Ø20
- Т3 — горячее водоснабжение, подача (ГВС), PP-R Ø20
- К1 — канализация бытовая
- направление уклона К1 / пола: Ø, мм на 1 м
- ревизия (прочистка) К1 — доступ сохранить
- тройник (ответвление к прибору)
- короб К1 над чистым полом (ГКЛВ под плитку)
- вывод В1 (код — в ведомости привязок)
- вывод Т3 (код — в ведомости привязок)
- вывод К1 (код — в ведомости привязок)
- сантехприбор по расстановке (габарит модели)
- стояк «Ст К1-N / Ст В1-N» (ГОСТ 21.601), Ø мм
- линия обрыва (граница фрагмента)
- граница фрагмента на плане (Фр. N)

Профиль выпусков К1 (до врезки в стояк)

Выпуск	Прибор	Ø	L, м	i, мм/м	Δh, мм	Прокладка, мм
К1-8	С_08 унитаз подвесной	Ø110	0,86	20	17	короб 160×140
К1-4	С_04 унитаз подвесной	Ø110	0,80	20	16	короб 160×140
К1-2	С_02 умывальник	Ø50	7,64	25	191	короб 280×110
К1-3	С_03 умывальник	Ø50	6,84	25	171	короб 260×110
К1-6	ОБ_04 стиральная машина	Ø50	5,94	25	149	короб 230×110
К1-7	С_07 душ	Ø50	3,89	25	97	короб 180×110
К1-1	С_01 ванна	Ø50	3,32	25	83	короб 170×110
К1-5	С_05 биде	Ø50	1,50	25	38	короб 120×110
К1-9	С_09 умывальник	Ø50	0,97	25	24	короб 110×110
К1-10	П11 мойка кухонная	Ø50	0,86	25	22	над полом за приборами
К1-11	П12 посудомоечная машина	Ø40	1,06	30	32	над полом за приборами

Короб h×b: h — от чистого пола, b — от чистовой стены. Стяжка 35 мм — лист полов.

Узел ввода В1, Т3 (схема, без масштаба)

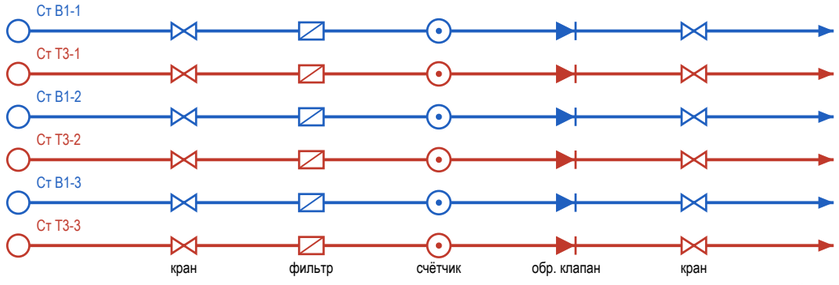

⊗ Ст К1-1, Ст К1-2, Ст К1-3 (кухня): ревизия на стояке — люк в коробе

Примечания

1. Трассы принципиальные, построены от стояков вдоль стен помещений; фактическое положение фиксируется исполнительной схемой с привязками (фото с рулеткой) до закрытия.
2. Уклон К1 не менее 1/d и не более 150 мм/м (СП 30.13330.2020, п. 19.1), приняты практические уклоны; поворот — двумя отводами 45°, ревизия после поворота, доступ сохранить. Стояк К1 в коробе — звукоизоляция стояка в коробе, без жёсткого контакта короба с трубой.
3. Решение по К1: стяжка 35 мм не укрывает трубы (нужно Ø + Δh + 45 мм) — выпуски идут над чистым полом вдоль стен: К1-10, К1-11 — за приборами и в раме инсталляции; К1-8, К1-4, К1-2, К1-3, К1-6, К1-7, К1-1, К1-5, К1-9 — в коробе ГКЛВ под плитку (размеры в профиле). Короба — на развёртках; отметку низа врезки в стояк замерить до черновых работ.
4. На каждом вводе В1 и Т3 — кран шаровой, фильтр, счётчик, обратный клапан; доступ через люк не меньше 300×400. Водопровод — в штробе стен или в коробах; трубы испытать давлением до закрытия (акт скрытых работ).
5. Расчёт систем, диаметры магистралей и подбор оборудования выполняет проектная организация; врезка и перенос стояков — по согласованию с управляющей организацией. Арматуру и привязки сверить по паспортам приборов.

					Проект: Квартира с кабинетом	
	Лист	№ док.	Подпись	Дата		
Дизайнер	Кырлан А.С.			21.10.26	Схема разводки водопровода и канализации	Стадия: П; Лист: 16; Листов: 97

Правка к этому листу


Поз.	Наименование и техническая характеристика	Тип, марка, обозначение документа	Код продукции	Поставщик	Ед. изм.	Кол.	Масса 1 ед., кг	Примечание
	Санитарные приборы							
1	Ванна акриловая 1700×800 мм, с каркасом, экраном и отверстием слив-перелив	ванна отдельностоящая овальная 1700×800, литой камень; смеситель напольный		выбор заказчика	шт	1		С_01
2	Унитаз подвесной безободковый, с сиденьем микролифт, крепёж и звукоизолирующая прокладка	Jacob Delafon Struktura EDF102-00		выбор заказчика	шт	2		С_04, С_08
3	Инсталляция для подвесного унитаза: рама высотой 1120 мм, бачок, клавиша смыва (ось клавиши 1050 мм от чистого пола)	аналог		выбор заказчика	шт	2		С_04, С_08; короб ГКЛВ
4	Умывальник подвесной 600×450 мм, с отверстием под смеситель и переливом	раковина накладная овальная на тумбе 1500 (1 из 2)		выбор заказчика	шт	2		С_02, С_03
5	Умывальник подвесной 540×400 мм, с отверстием под смеситель и переливом	раковина 540 на консоли, травертин		выбор заказчика	шт	1		С_09
6	Биде подвесное	аналог		выбор заказчика	шт	1		С_05
7	Поддон душевой низкий 900×1500 мм, с сифоном и выпуском Ø50, на ножках/подиуме	душ с трапом и стеклянной перегородкой		выбор заказчика	шт	1		С_07
8	Мойка кухонная 800×600 мм, с переливом	аналог		с кухонной мебелью	шт	1		П11
9	Полотенцесушитель электрический, IP44, с терморегулятором	аналог		выбор заказчика	шт	1		С_06
	Смесители, сифоны и арматура приборов							
10	Смеситель для ванны настенный однорычажный, межосевое 150 мм, с душевым набором (лейка, шланг, держатель)	аналог		выбор заказчика	шт	1		С_01
11	Смеситель для умывальника однорычажный, с донным клапаном	аналог		выбор заказчика	шт	3		С_02, С_03, С_09
12	Душевая система скрытого монтажа с термостатом: встраиваемая часть, верхний душ, ручная лейка	аналог		выбор заказчика	шт	1		С_07; встраиваемая часть — до плитки
13	Смеситель кухонный однорычажный, высокий излив	аналог		выбор заказчика	шт	1		П11
14	Обвязка ванны слив-перелив Ø40/50 с сифоном	аналог		выбор заказчика	шт	1		С_01
15	Сифон для умывальника бутылочный Ø32/40–50, с гофрой к выпуску	аналог		выбор заказчика	шт	3		С_02, С_03, С_09
16	Сифон для мойки с отводом для ПММ Ø40/50	аналог		выбор заказчика	шт	1		П11
17	Сифон для стиральной машины встраиваемый в стену Ø50, с обратным клапаном	аналог		выбор заказчика	шт	1		ОБ_04
18	Кран угловой ½"×½" с гибкой подводкой 40 см (умывальники, мойка)	аналог		выбор заказчика	шт	8		по 2 на прибор
19	Кран шаровой угловой ½"×¾" для подключения стиральной и посудомоечной машины	аналог		выбор заказчика	шт	2		ОБ_04, П12
	Трубопроводы							
20	Труба полипропиленовая PP-R PN20 Ø20×3,4 (В1)	ГОСТ 32415-2013		выбор заказчика	м	25	0,17	15,5 + 7,0 + 10 %
21	Труба PP-R, армированная стекловолокном, PN20 Ø20×2,8 (Т3)	ГОСТ 32415-2013		выбор заказчика	м	19,5	0,15	14,0 + 3,6 + 10 %
22	Труба канализационная ПП Ø40 (К1)	ГОСТ 32414-2013		выбор заказчика	м	1		0,3 + 0,6 + 10 %
23	Труба канализационная ПП Ø50 (К1)	ГОСТ 32414-2013		выбор заказчика	м	16,5		12,0 + 2,8 + 10 %
24	Труба канализационная ПП Ø110 (К1)	ГОСТ 32414-2013		выбор заказчика	м	2,5		1,7 + 0,4 + 10 %
	Фасонные части и выводы							
25	Отвод канализационный ПП 45° Ø40	ГОСТ 32414-2013		выбор заказчика	шт	2		2 шт. на поворот
26	Отвод канализационный ПП 45° Ø50	ГОСТ 32414-2013		выбор заказчика	шт	18		2 шт. на поворот
27	Отвод канализационный ПП 45° Ø110	ГОСТ 32414-2013		выбор заказчика	шт	12		2 шт. на поворот
28	Тройник канализационный ПП 45° (врезки ветвей)	ГОСТ 32414-2013		выбор заказчика	шт	10		
29	Ревизия канализационная ПП (после поворота трассы)	ГОСТ 32414-2013		выбор заказчика	шт	9		доступ сохранить
30	Фитинги PP-R Ø20: тройники, угольники 90° (ветви и повороты В1, Т3)	ГОСТ 32415-2013		выбор заказчика	шт	44		
31	Водорозетка PP-R Ø20×½" настенная, с креплением	ГОСТ 32415-2013		выбор заказчика	шт	18		коды — лист выводов
	Узлы ввода, люки, короба							
32	Кран шаровой латунный Ду15 PN16 (отключение ввода)	аналог		выбор заказчика	шт	6		Ст В1-1, Ст Т3-1, Ст В1-2, Ст Т3-2, Ст В1-3, Ст Т3-3
33	Фильтр сетчатый косой Ду15	аналог		выбор заказчика	шт	6		
34	Счётчик воды крыльчатый Ду15 (ХВ, ГВ), с поверкой	аналог		выбор заказчика	шт	6		пломба УК
35	Клапан обратный Ду15	аналог		выбор заказчика	шт	6		
36	Люк ревизионный нажимной под плитку 300×400 мм	аналог		выбор заказчика	шт	2		к стоякам и арматуре
37	Звукоизоляция стояка К1 в коробе: рулонный звукоизоляционный материал ≥ 10 мм, обмотка стояка на высоту этажа	аналог		выбор заказчика	м	8,1		Ст К1-1, Ст К1-2, Ст К1-3 (кухня)
38	Короб К1 над полом: профиль ПН/ПС, ГКЛВ 12,5 мм под плитку	аналог		выбор заказчика	м	15,2		сечение — лист разводки

Примечания

1. Форма 1 ГОСТ 21.110-2013, ширины граф изменены по п. 4.1. «Аналог» — аналог по характеристикам: модели внести до черновых работ, привязки выводов сверить по паспортам.
2. Бытовая техника не входит (показана арматура подключения), мойка — в комплекте кухни. Длины труб — трасса листа разводки + подъёмы + 10 %.
3. Стояк К1 в коробе — звукоизоляция стояка в коробе без жёсткого контакта короба с трубой.
4. Расчёт систем водоснабжения и канализации, диаметры магистралей и подбор оборудования выполняет проектная организация.

					Проект: Квартира с кабинетом		
	Лист	№ док.	Подпись	Дата	Спецификация сантехнического оборудования	Стадия	Лист	Листов
Дизайнер	Кырлан А.С.			21.10.26		П	17	97

Правка к этому листу

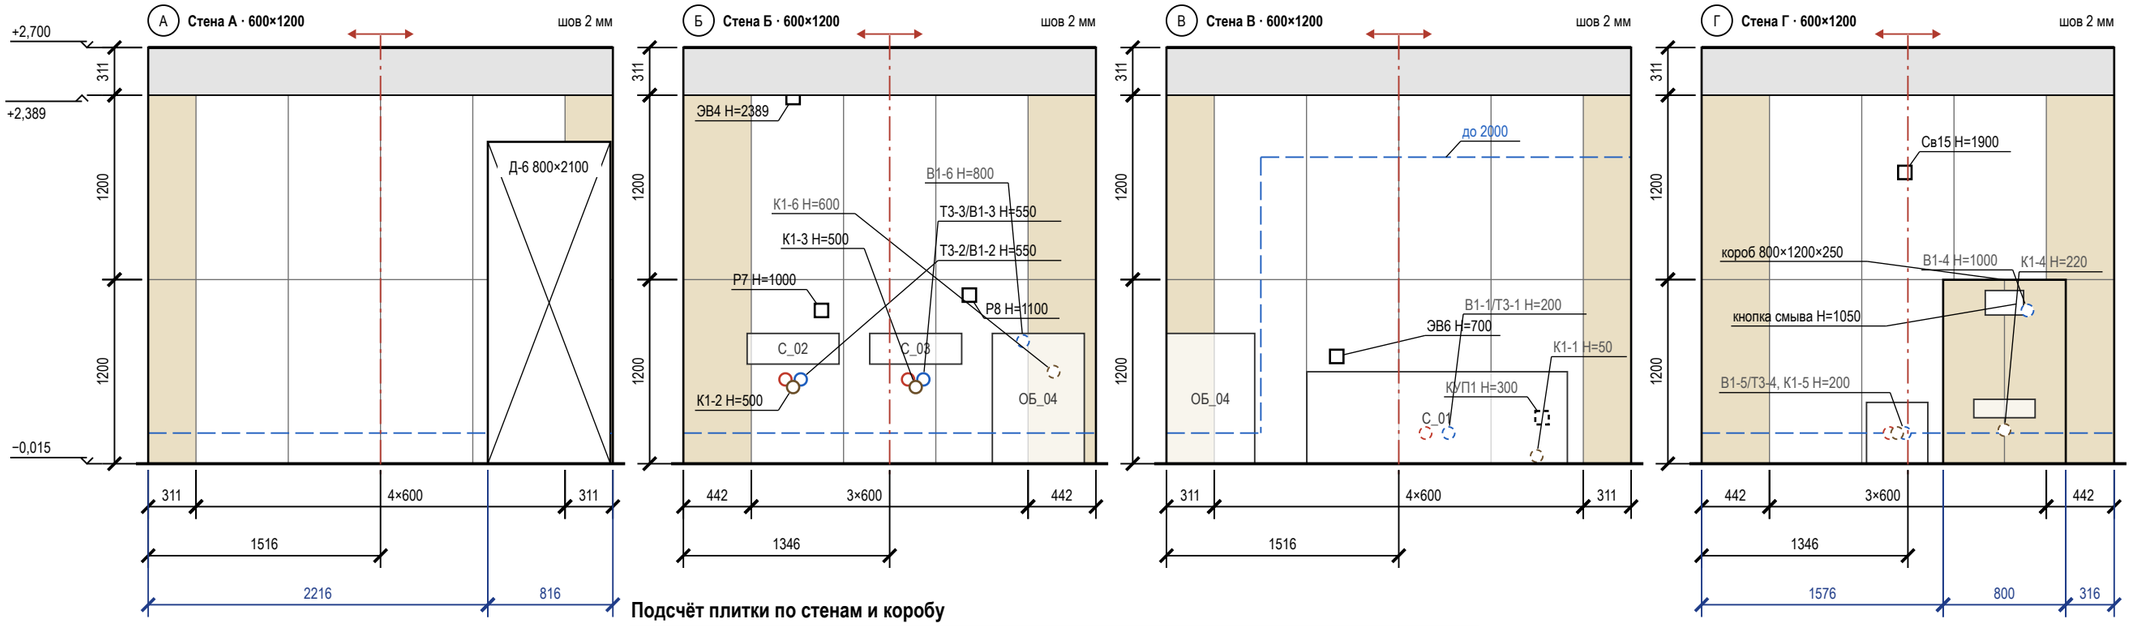

Условные обозначения

- плитка целая; тонкая линия — шов
- плитка с подрезкой (размер — на цепочке)
- ось старта; стрелки — направление укладки
- верх гидроизоляции: 200 от ЧП, в мокрой зоне — «до …»
- проём — не облицовывается
- сантехприбор: габарит, высота по практике
- короб инсталляции, в нём кнопка смыва 250×160
- вывод В1 (код — в ведомости привязок)
- вывод Т3 (код — в ведомости привязок)
- вывод К1 (код — в ведомости привязок)
- вывод за прибором / в коробе (не на сетке)
- электроточка: марка и Н — по листам ЭОМ
- отметка уровня, м: ±0,000 — чистый пол жилых помещений
- низ потолка; серая полоса — стена без плитки
- (А) обозначение стены А–Г (как на развёртках)

Подсчёт плитки по стенам и коробу

Поверхность	L × H, мм	S, м²	Целых	Подр.	С запасом	Подрезки: край / верх, мм
стена А	3032 × 2404	5,72	6	6	14	311 / 311; целый ряд
стена Б	2692 × 2404	6,59	6	4	11	442 / 442; целый ряд
стена В	3032 × 2404	7,40	8	4	14	311 / 311; целый ряд
стена Г	2692 × 2404	5,63	4	5	10	442 / 442; целый ряд
короб (ст. Г)	800×1200×250	1,76	0	6	7	лицо 399 / 399; бок. 250
Итого		**27,10**	**24**	**25**	**56**	

Сдвиг точек под раскладку

Точка (ВК, ЭОМ)	Стена	Проект: от угла / Н	Под раскладку: от угла / Н	Сдвиг, мм
Т3-2/В1-2, К1-2	Б	716 / 550, 500	744 / 550, 500	+28 в центр плитки
Т3-3/В1-3, К1-3	Б	1516 / 550, 500	1647 / 550, 500	+131 на шов
Р7	Б	901 / 1000	1045 / 1000	+144 на шов
Р8	Б	1866 / 1100	1948 / 1100	+82 в центр плитки
ЭВ4	Б	716 / 2389	744 / 2403	+28 в центр плитки; Н +14
ЭВ6	В	1111 / 700	1215 / 700	+104 в центр плитки
Св15	Г	1326 / 1900	1346 / 1900	+20 в центр плитки

Примечания


1. Вид изнутри, стены по часовой стрелке А → Г. Высоты — от чистого пола (−0,015), отметки — от ±0,000. Раскладка от чистовых размеров (штукатурка 10 + клей 5 + плитка 9 мм), подрезки чистые; старт — от оси стены, ряды от пола целыми.
2. Верх плитки +2,389, потолок +2,700, зазор 311 мм: потолок ГКЛ опустить до +2,392 (шов 3 мм, герметик) — согласовать с монтажником ГКЛ; иначе профиль-окантовка, полосу окрасить в цвет потолка. Подрезной ряд 306 мм не делать.
3. Точки из таблицы сдвигов переносятся до черновой разводки: смеситель — по оси пары В1 + Т3; вывод на оси прибора — вместе с прибором, иначе старт раскладки — на ось прибора.
4. За приборами и в коробе (В1-6, К1-6, В1-1/Т3-1, К1-1, КУП1, В1-4, К1-4, В1-5/Т3-4, К1-5) — штриховым кольцом.
5. Гидроизоляция: 200 мм от ЧП по периметру; над ванной — до 2000 и 300 мм за борт (СП 29.13330.2011, п. 7.2 — на высоту замачивания); углы — лентой; акт скрытых работ, пролив.
6. Короб 800×1200×250: лицо 399 / 399 мм от оси кнопки смыва, боковины, полка; углы — запил 45° или профиль; за коробом плитку не кладут.

					Проект: Квартира с кабинетом
	Лист	№ док.	Подпись	Дата	Раскладка плитки. Ванная. Развёртки стен
Дизайнер	Кырлан А.С.			21.10.26	

Стадия	Лист	Листов
П	18	97

выпуск 18.10.2026 № 918b20bf25 · стр. 18 из 97

Правка к этому листу

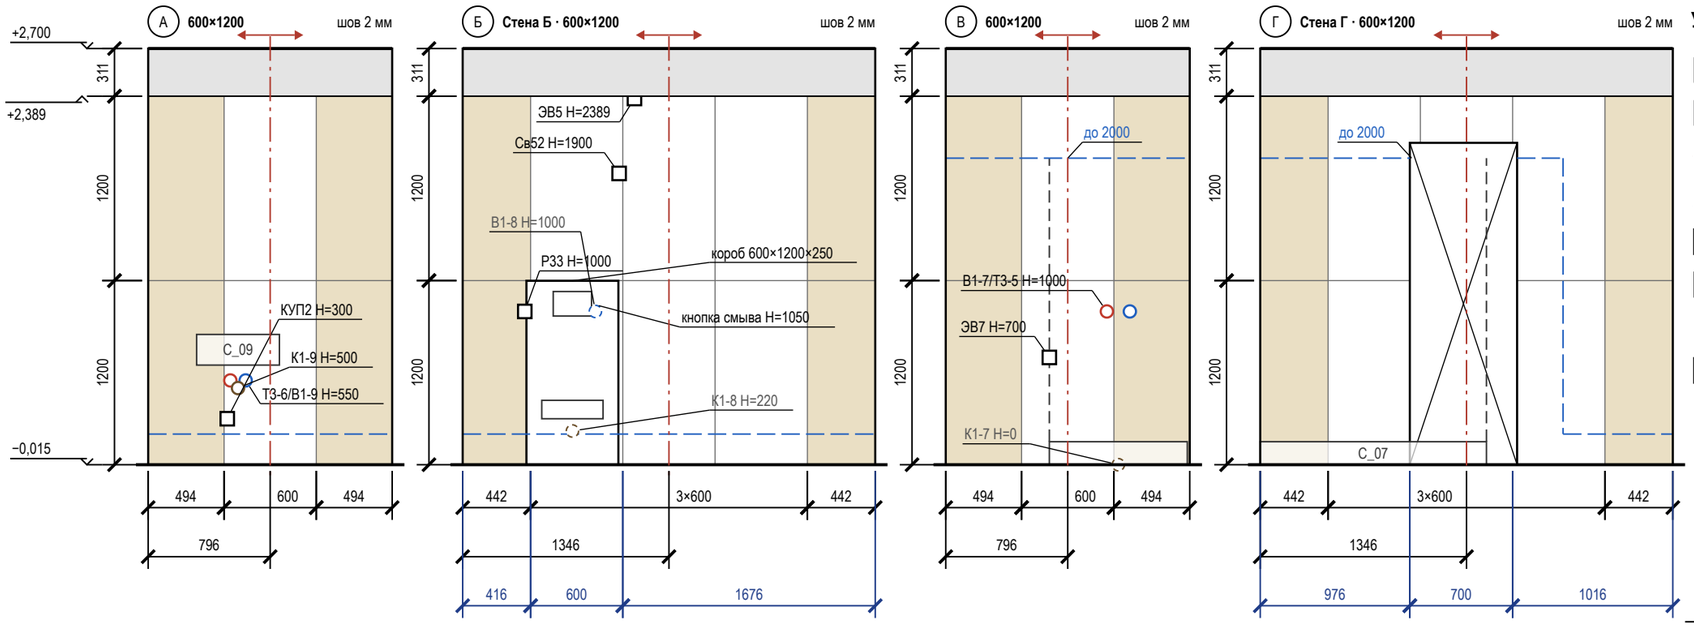

Условные обозначения

- плитка целая; тонкая линия — шов
- плитка с подрезкой (размер — на цепочке)
- ось старта; стрелки — направление укладки
- верх гидроизоляции: 200 от ЧП, в мокрой зоне — «до …»
- проём — не облицовывается
- сантехприбор: габарит, высота по практике
- граница душевой зоны (ограждение)
- короб инсталляции, в нём кнопка смыва 250×160
- вывод В1 (код — в ведомости привязок)
- вывод Т3 (код — в ведомости привязок)
- вывод К1 (код — в ведомости привязок)
- вывод за прибором / в коробе (не на сетке)
- электроточка: марка и Н — по листам ЭОМ
- отметка уровня, м: ±0,000 — чистый пол жилых помещений
- низ потолка; серая полоса — стена без плитки
- А обозначение стены А–Г (как на развёртках)

Подсчёт плитки по стенам и коробу

Поверхность	L × H, мм	S, м²	Целых	Подр.	С запасом	Подрезки: край / верх, мм
стена А	1592 × 2404	3,94	2	4	7	494 / 494; целый ряд
стена Б	2692 × 2404	5,87	5	5	11	442 / 442; целый ряд
короб (ст. Б)	600×1200×250	1,47	1	3	5	лицо 600; бок. 250
стена В	1592 × 2404	3,94	2	4	7	494 / 494; целый ряд
стена Г	2692 × 2404	5,12	0	9	10	442 / 442; целый ряд
Итого		**20,34**	**10**	**25**	**40**	

Сдвиг точек под раскладку

Точка (ВК, ЭОМ)	Стена	Проект: от угла / Н	Под раскладку: от угла / Н	Сдвиг, мм
Т3-6/В1-9, К1-9	А	586 / 550, 500	495 / 550, 500	−91 на шов
КУП2	А	516 / 300	495 / 300	−21 на шов
Р33	Б	405 / 1000	443 / 1000	+38 на шов
Св52	Б	1021 / 1900	1045 / 1900	+24 на шов
ЭВ5	Б	1121 / 2389	1045 / 2343	−76 на шов; Н −46
В1-7/Т3-5	В	1126 / 1000	1097 / 1000	−29 на шов
ЭВ7	В	676 / 700	796 / 700	+120 в центр плитки

Примечания


1. Вид изнутри, стены по часовой стрелке А → Г. Высоты — от чистого пола (−0,015), отметки — от ±0,000. Раскладка от чистовых размеров (штукатурка 10 + клей 5 + плитка 9 мм), подрезки чистые; старт — от оси стены, ряды от пола целыми.
2. Верх плитки +2,389, потолок +2,700, зазор 311 мм: потолок ГКЛ опустить до +2,392 (шов 3 мм, герметик) — согласовать с монтажником ГКЛ; иначе профиль-окантовка, полосу окрасить в цвет потолка. Подрезной ряд 306 мм не делать.
3. Точки из таблицы сдвигов переносятся до черновой разводки: смеситель — по оси пары В1 + Т3; вывод на оси прибора — вместе с прибором, иначе старт раскладки — на ось прибора.
4. За приборами и в коробе (В1-8, К1-8, К1-7) — штриховым кольцом.
5. Гидроизоляция: 200 мм от ЧП по периметру; у душа — до 2000 и 500 мм за поддон (СП 29.13330.2011, п. 7.2 — на высоту замачивания); углы — лентой; акт скрытых работ, пролив.
6. Короб 600×1200×250: лицо 600 мм от оси кнопки смыва, боковины, полка; углы — запил 45° или профиль; за коробом плитку не кладут.

					Проект: Квартира с кабинетом
	Лист	№ док.	Подпись	Дата	Раскладка плитки. Санузел гостевой. Развёртки стен
Дизайнер	Кырлан А.С.			21.10.26	

Стадия	Лист	Листов
П	19	97

выпуск 18.10.2026 № 918b20bf25 · стр. 19 из 97

Правка к этому листу

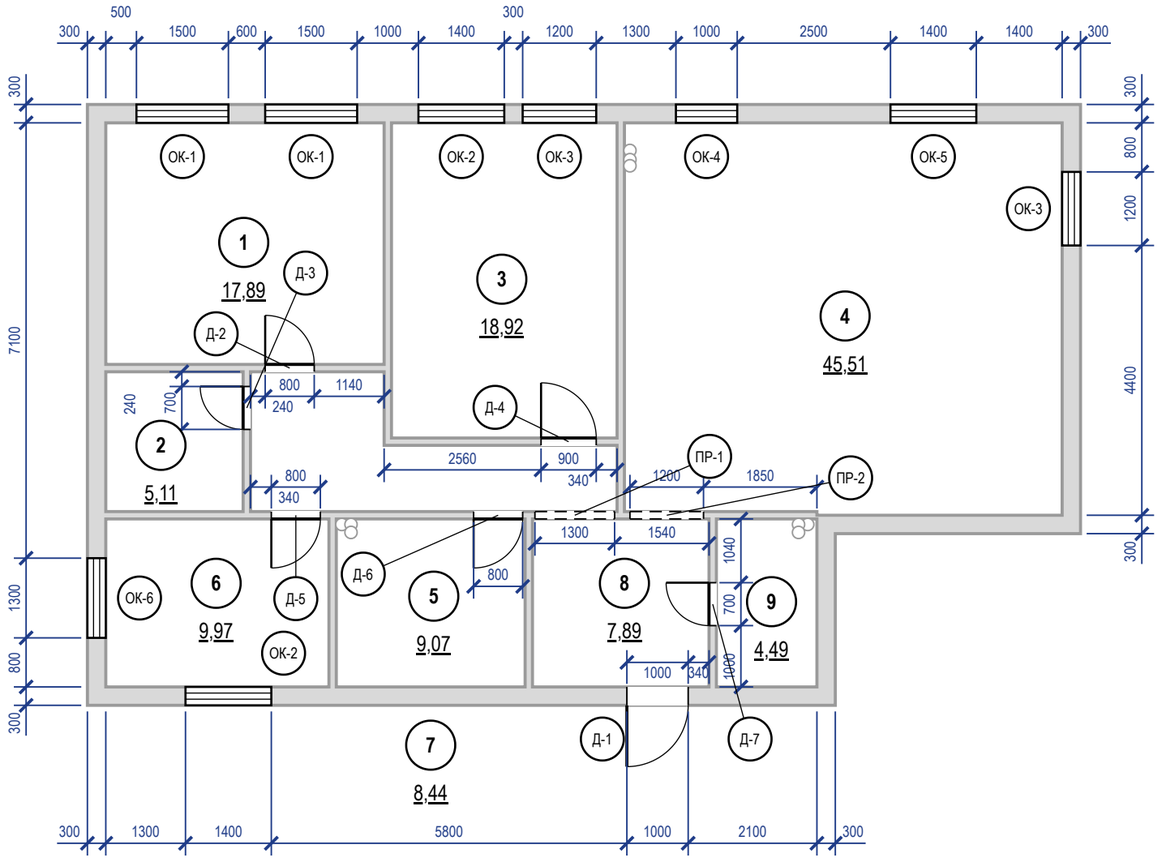

Ведомость заполнения проёмов

Марка	Наименование, обозначение	Проём ш×в, мм	Кол.	Откр.	Отделка полотна	Фурнитура	Прим.
Д-1	Блок дверной входной, ГОСТ 31173-2016	1000×2100	1	Л	в комплекте блока	в комплекте блока (замки, глазок)	наружу
Д-2	Дверь скрытого монтажа, ТУ изготовителя	800×2100	1	П	окраска No. 15 с двух сторон	скрытые петли 3D, магнитный замок	
Д-3	Дверь скрытого монтажа, ТУ изготовителя	700×2100	1	Л	V503 — пом. 2, No. 15 — пом. 5	скрытые петли 3D, магнитный замок	
Д-4	Дверь скрытого монтажа, ТУ изготовителя	900×2100	1	П	окраска No. 15 с двух сторон	скрытые петли 3D, магнитный замок	
Д-5	Дверь скрытого монтажа, ТУ изготовителя	800×2100	1	Л	окраска No. 15 с двух сторон	скрытые петли 3D, магнитный замок	
Д-6	Дверь скрытого монтажа, ТУ изготовителя	800×2100	1	Л	в тон облицовки — пом. 7, No. 15 — пом. 5	скрытые петли 3D, магнитный замок, фиксатор WC	порог 15
Д-7	Дверь скрытого монтажа, ТУ изготовителя	700×2100	1	Л	No. 15 — пом. 8, в тон облицовки — пом. 9	скрытые петли 3D, магнитный замок, фиксатор WC	порог 15
ПР-1	Портал без заполнения	1300×2100	1				б/п
ПР-2	Портал без заполнения	1200×2100	1				б/п
ОК-1	Блок оконный, ГОСТ 23166-2021	1500×1600	2				низ 800
ОК-2	Блок оконный, ГОСТ 23166-2021	1400×1600	2				низ 800
ОК-3	Блок оконный, ГОСТ 23166-2021	1200×1600	2				низ 800
ОК-4	Блок оконный, ГОСТ 23166-2021	1000×1400	1				низ 1000
ОК-5	Блок оконный, ГОСТ 23166-2021	1400×1600	1				низ 900
ОК-6	Блок оконный, ГОСТ 23166-2021	1300×1600	1				низ 800


Примечания

1. Размеры проёмов и привязки — в миллиметрах от чистых граней стен до отделки; привязка — от угла того помещения, со стороны которого стоит размер. Размер в ведомости — ширина × высота проёма от чистого пола 0,000. Откос от угла помещения до проёма с коробкой — не менее 50 мм.
2. Марки в кружках — типы заполнения проёмов (ГОСТ 21.501-2018, п. 5.3.2); одна марка — один типоразмер; количество сверено с планом.
3. Открывание: Л — петли слева, П — справа, если смотреть со стороны, куда открывается полотно (на себя).
4. Скрытые двери (Д-2…Д-7): проём замерить в чистоте; блок заказать до штукатурки (≈ 30 дн.), короб ставить до штукатурки; полотно навесить после чистовой отделки, красить в цвет стен. Порядок практика монтажа, изготовитель подтверждает.
5. Д-2…Д-7 — существующие проёмы, до техзаключения не расширять.
6. Размеры проёмов и привязки сняты со скана плана заказчика и на объекте не замерены (обмерный план — лист 3).
7. Экспликация помещений — лист 3; в марках помещений — номер и площадь, м².
8. Привязка проёма к углу помещения меньше 1 мм на листе, размер на плане не показан: Д-6 — 40 мм; ПР-1 — 40 мм; ПР-2 — 90 мм.

					Проект: Квартира с кабинетом			
	Лист	№ док.	Подпись	Дата	План размещения дверей	Стадия	Лист	Листов
Дизайнер	Кырлан А.С.			21.10.26		П	20	97

выпуск 18.10.2026 № 918b20bf25 · стр. 20 из 97

Правка к этому листу

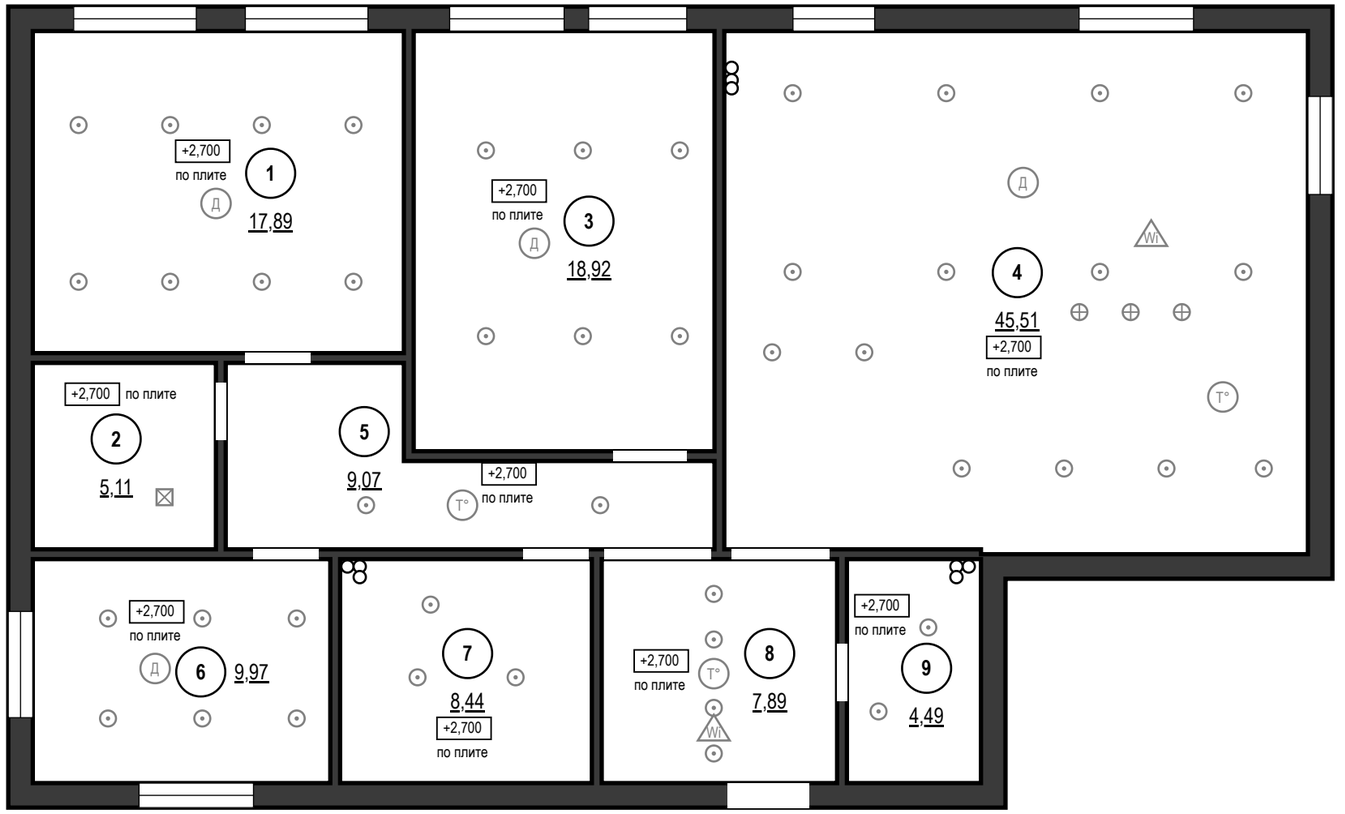

Ведомость потолков

Пом.	Марка	Конструкция	Низ / верх ниши	S, м²	Q
1		по плите, окраска	+2,700	17,89	
2		по плите, окраска	+2,700	5,11	
3		по плите, окраска	+2,700	18,92	
4		по плите, окраска	+2,700	45,51	
5		по плите, окраска	+2,700	9,07	
6		по плите, окраска	+2,700	9,97	
7		по плите, окраска	+2,700	8,44	
8		по плите, окраска	+2,700	7,89	
9		по плите, окраска	+2,700	4,49	
		Итого		**127,29**	

Ведомость вырезов и закладных в потолке

Марка	Устройство	Кол.	Пом.
	Светильник встраиваемый (марки — план освещения)	45	1, 3, 4, 5, 6, 7, 8, 9
	Светильник накладной (марки — план освещения)	1	2
	Светильник подвесной (марки — план освещения)	3	4
ИП1, ИП2, ИП4, ИП2	Извещатель дымовой	4	1, 3, 4, 6
ИП5, ИП6, ИП3	Извещатель тепловой	3	4, 5, 8
AP2, AP1	Точка доступа Wi-Fi, PoE	2	4, 8

Примечания


1. За отметку ±0,000 принят уровень чистого пола сухих помещений (готовое покрытие), а не существующего пола; пол пом. 7, 9 — −0,015; верх плиты перекрытия −0,064 — расчётный по пирогу пола, не замерен; существующий пол снимается до плиты, его отметка не замерена. Отметки в прямоугольниках — низ потолка; низ плиты перекрытия +2,700. Марка потолка — одна конструкция и отметка на весь альбом.
2. Светильники и потолочные устройства — подложка с планов освещения, слаботочных систем и вентиляции (положение — по ним); вырезы и закладные — по ведомости на листе, до обшивки; отверстия не совмещать с профилями.
3. Пом. 1, 2, 3, 4, 5, 6, 7, 8, 9 — потолок по плите без подвесной системы; отделка — по ведомости отделки.

					Проект: Квартира с кабинетом
	Лист	№ док.	Подпись	Дата	
Дизайнер	Кырлан А.С.			21.10.26	План потолков

Стадия	Лист	Листов
П	21	97

выпуск 18.10.2026 № 918b20bf25 · стр. 21 из 97

Правка к этому листу

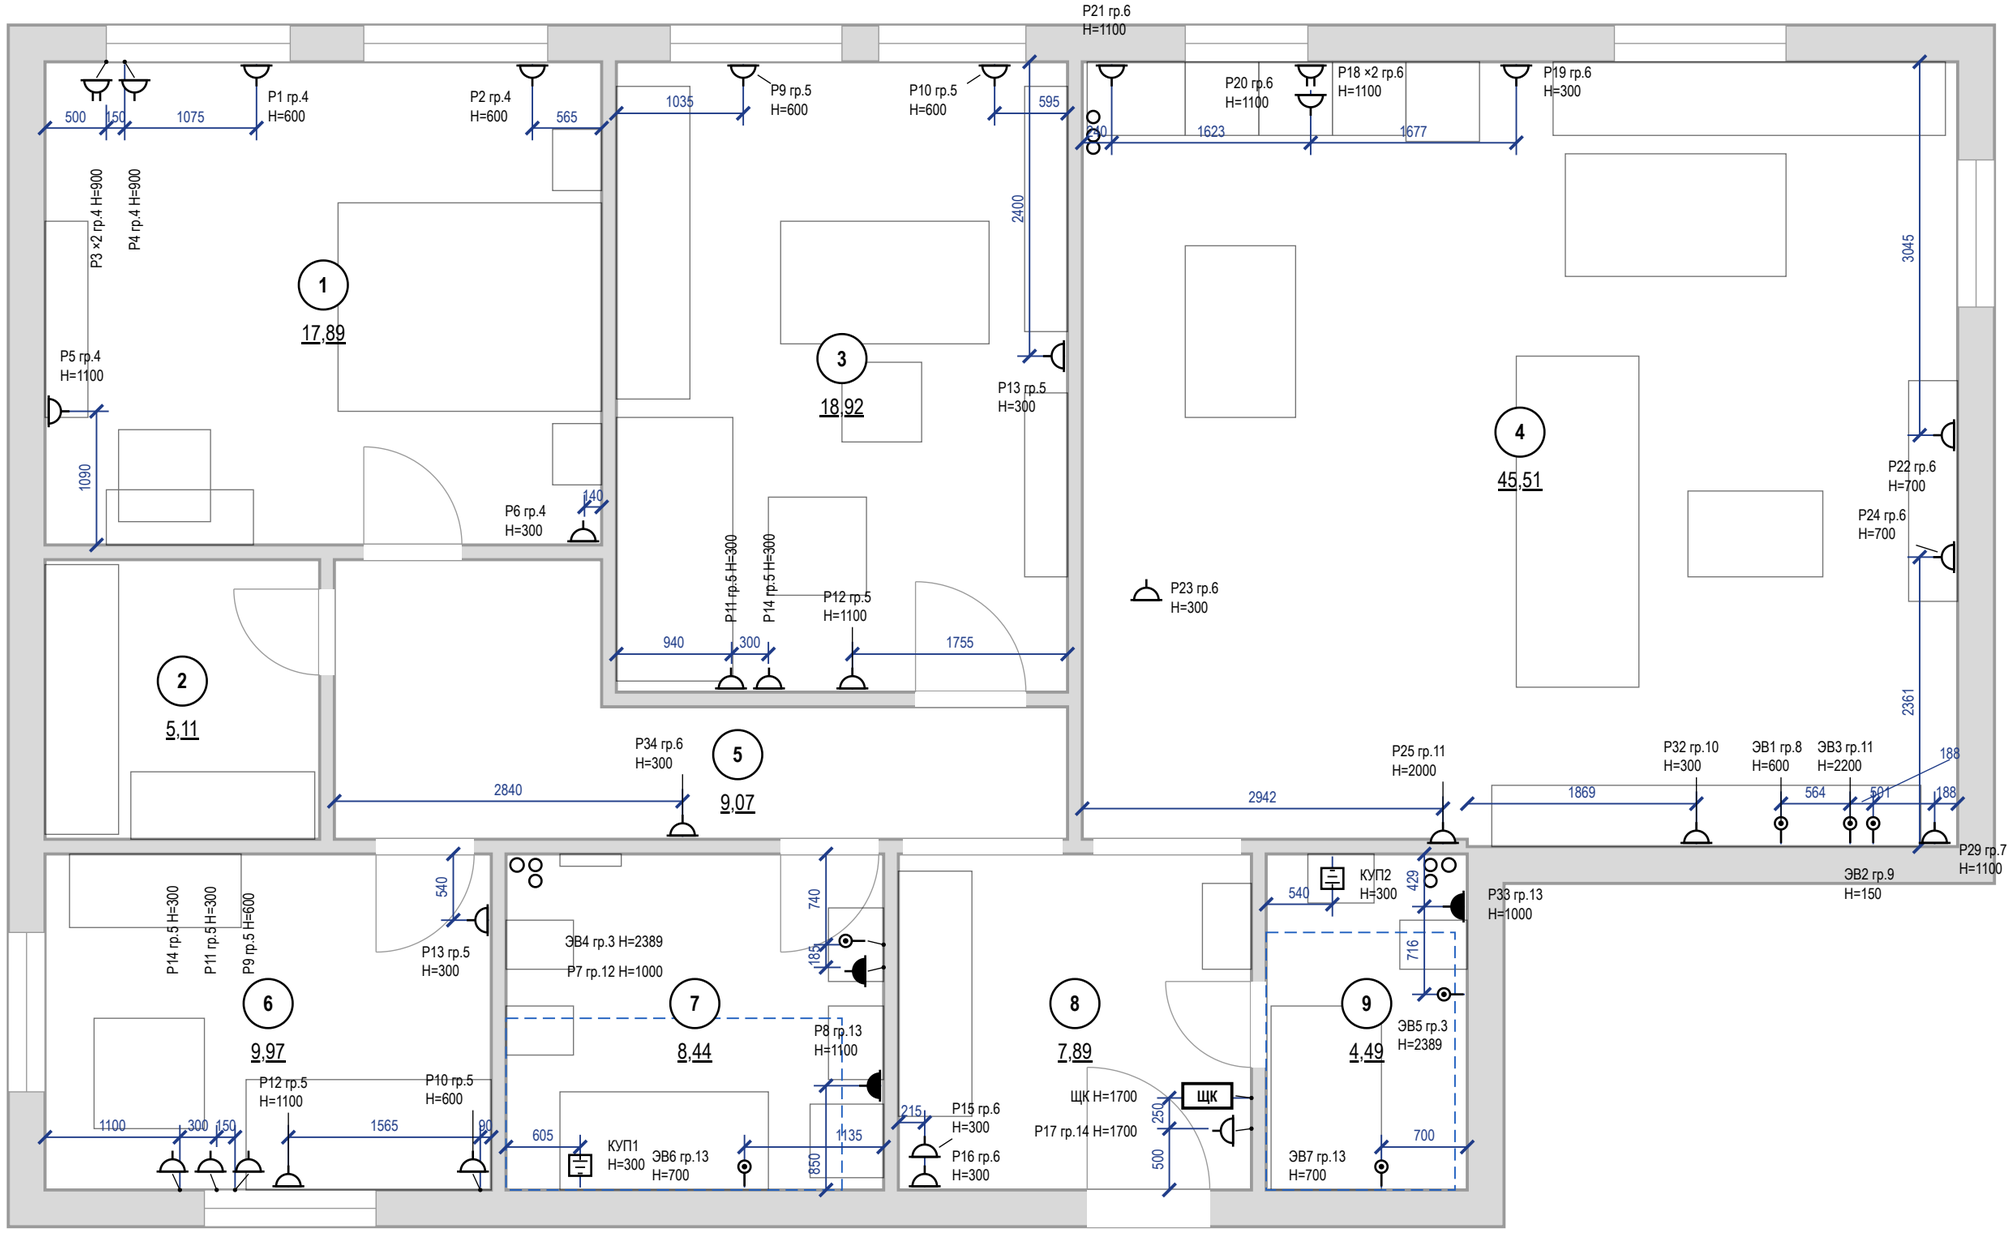


Примечания

1. За отметку 0,000 принят уровень чистого пола. Высоты H — от чистого пола до оси изделия; привязки — от чистовой грани стены до оси механизма (у рамки на несколько постов — до оси рамки).
2. Высота установки, не указанная на плане: розетки — 300 мм от чистого пола; выводы кабеля — по паспорту прибора.
3. Розетки в санузле — только вне зон 0–2 (ПУЭ 7.1.48, ГОСТ Р 50571.7.701-2024), IP44, через УЗО 30 мА.
4. Розеточные и мокрые линии — через УЗО или дифавтомат с током утечки не более 30 мА (ПУЭ 7.1.79); в санузле выполнить ДСУП (ПУЭ 7.1.87–7.1.88).
5. Кабель — медный, исполнение нг(A)-LS (ГОСТ 31565-2012); скрытая прокладка только горизонтально и вертикально, фактические трассы зафиксировать исполнительной схемой до закрытия отделкой.
6. Расчёт нагрузок, токов КЗ, селективности и сечений — по проекту ЭОМ организации с допуском СРО; лист задаёт состав, расположение и группы.
7. Выводы кухонной техники — после утверждения проекта кухни (ориентировочно); привязки выводов даны от осей модулей гарнитура и пересматриваются вместе с проектом кухни.
8. Электрический тёплый пол проектом не предусмотрен; при решении заказчика устроить — отдельный лист «План тёплых полов»: контуры с отступом 100 мм от стен и мебели без ножек, датчик в гофре, терморегулятор, своя группа щита через УЗО 30 мА.
9. Ведомости электроточек, изделий, светильников и расшифровка клавиш — лист «Ведомость электроточек и изделий».

					Проект: Квартира с кабинетом		
	Лист	№ док.	Подпись	Дата	План розеток и электровыводов	Стадия	Лист	Листов
Дизайнер	Кырлан А.С.			21.10.26		П	22	97

выпуск 18.10.2026 № 918b20bf25 · стр. 22 из 97

Правка к этому листу

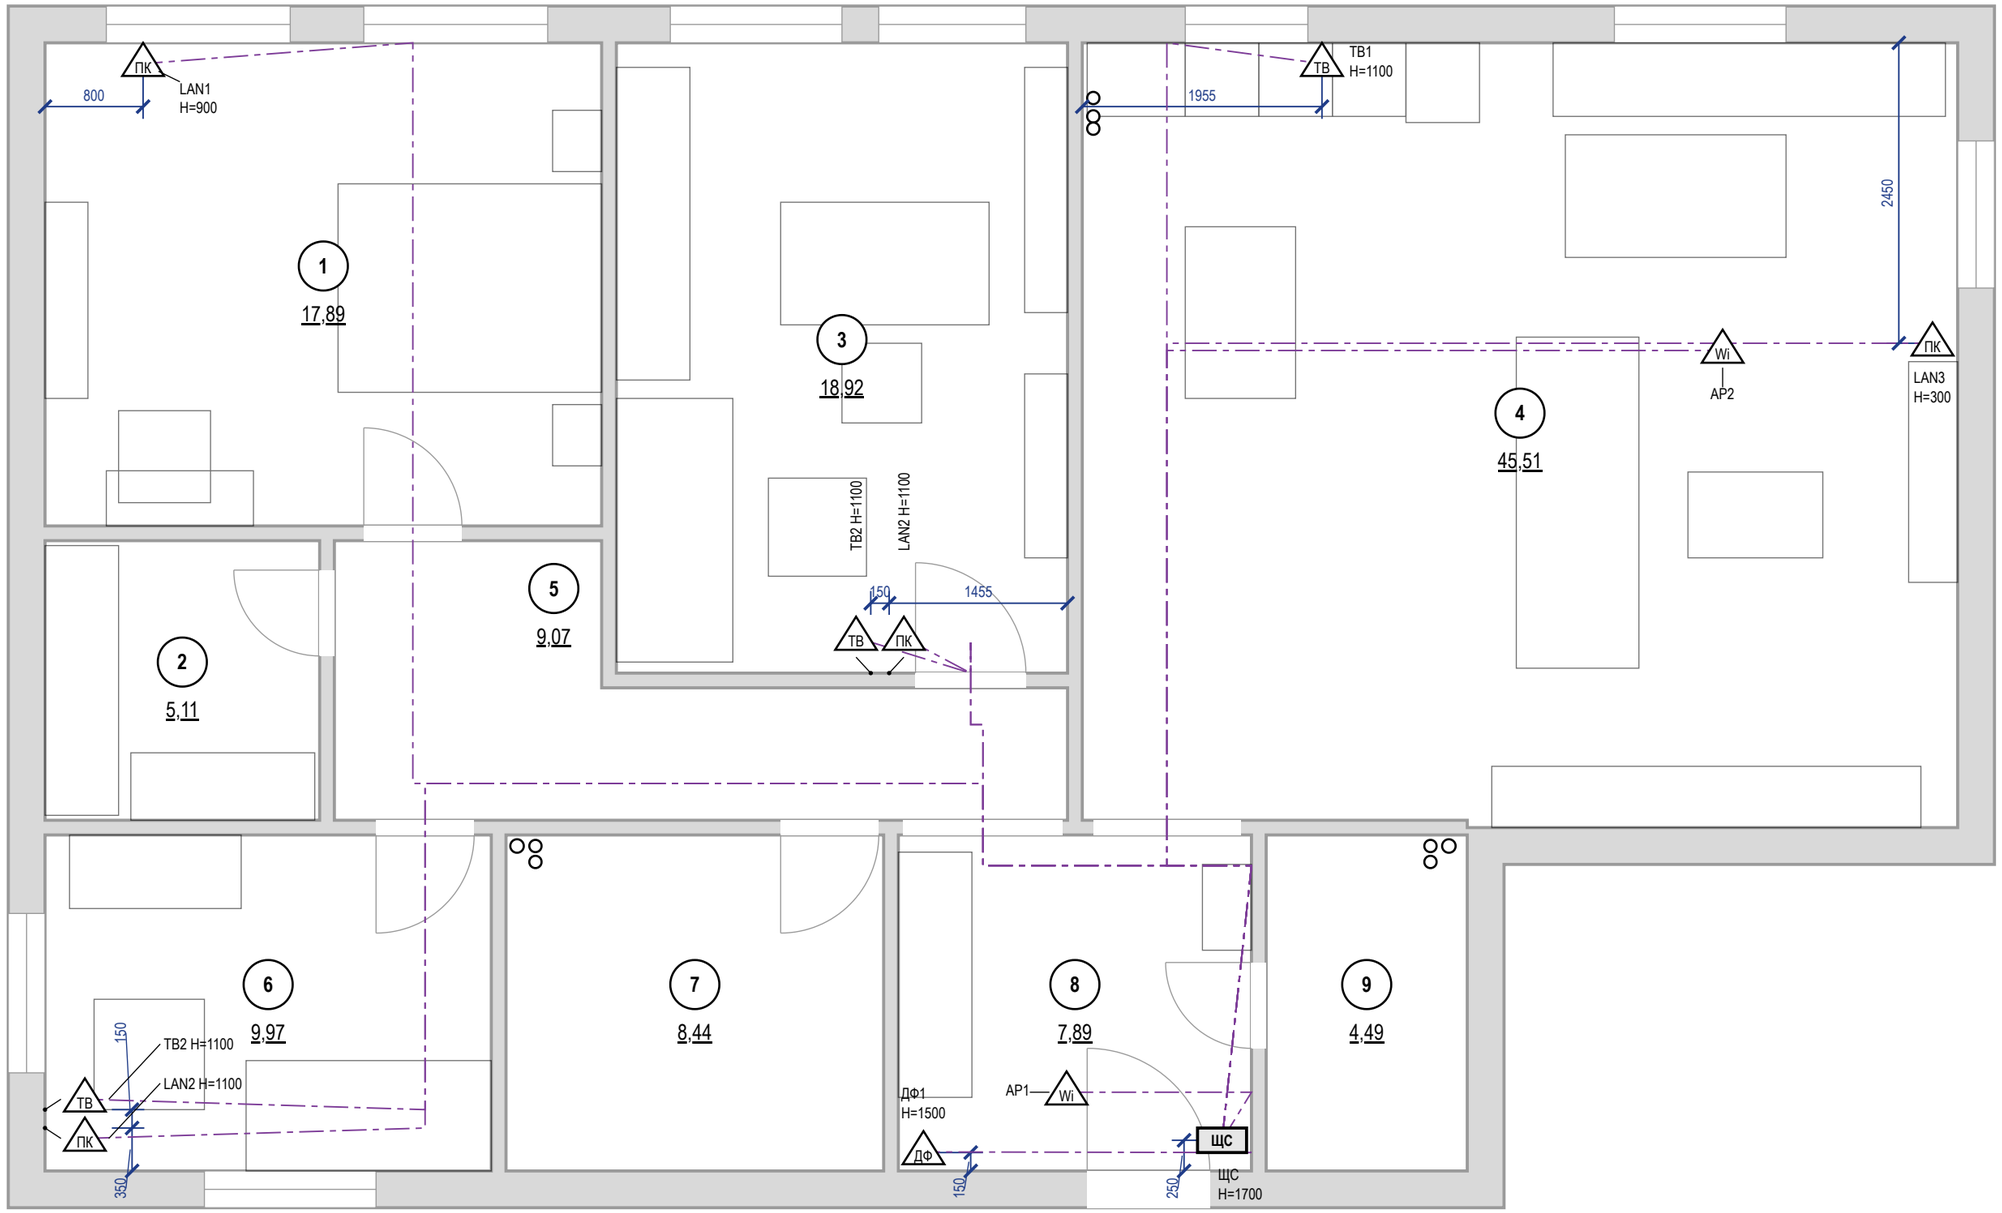

Примечания


1. За отметку 0,000 принят уровень чистого пола. Высоты H — от чистого пола до оси изделия; привязки — от чистовой грани стены до оси механизма (у рамки на несколько постов — до оси рамки).
2. Высота установки, не указанная на плане: розетки LAN и ТВ — 300 мм от чистого пола.
3. Слаботочные кабели — отдельно от силовых: в своей трубе или лотке, при параллельной прокладке не ближе 100 мм к силовым, пересечения под прямым углом; каждую точку — отдельным кабелем от ЩС без скруток.
4. Трассы на листе — принципиальные; фактические зафиксировать исполнительной схемой до закрытия отделкой. Силовые линии, УЗО 30 мА, ДСУП, кабель нг(A)-LS — по листам розеток и щита.
5. Проект силовой части и расчёт токов КЗ — по проекту ЭОМ; слаботочная часть согласуется с провайдером и управляющей компанией (домофон, коллективное ТВ).

					Проект: Квартира с кабинетом
	Лист	№ док.	Подпись	Дата	План слаботочных сетей
Дизайнер	Кырлан А.С.			21.10.26	

Стадия	Лист	Листов
П	23	97

выпуск 18.10.2026 № 918b20bf25 · стр. 23 из 97

Правка к этому листу

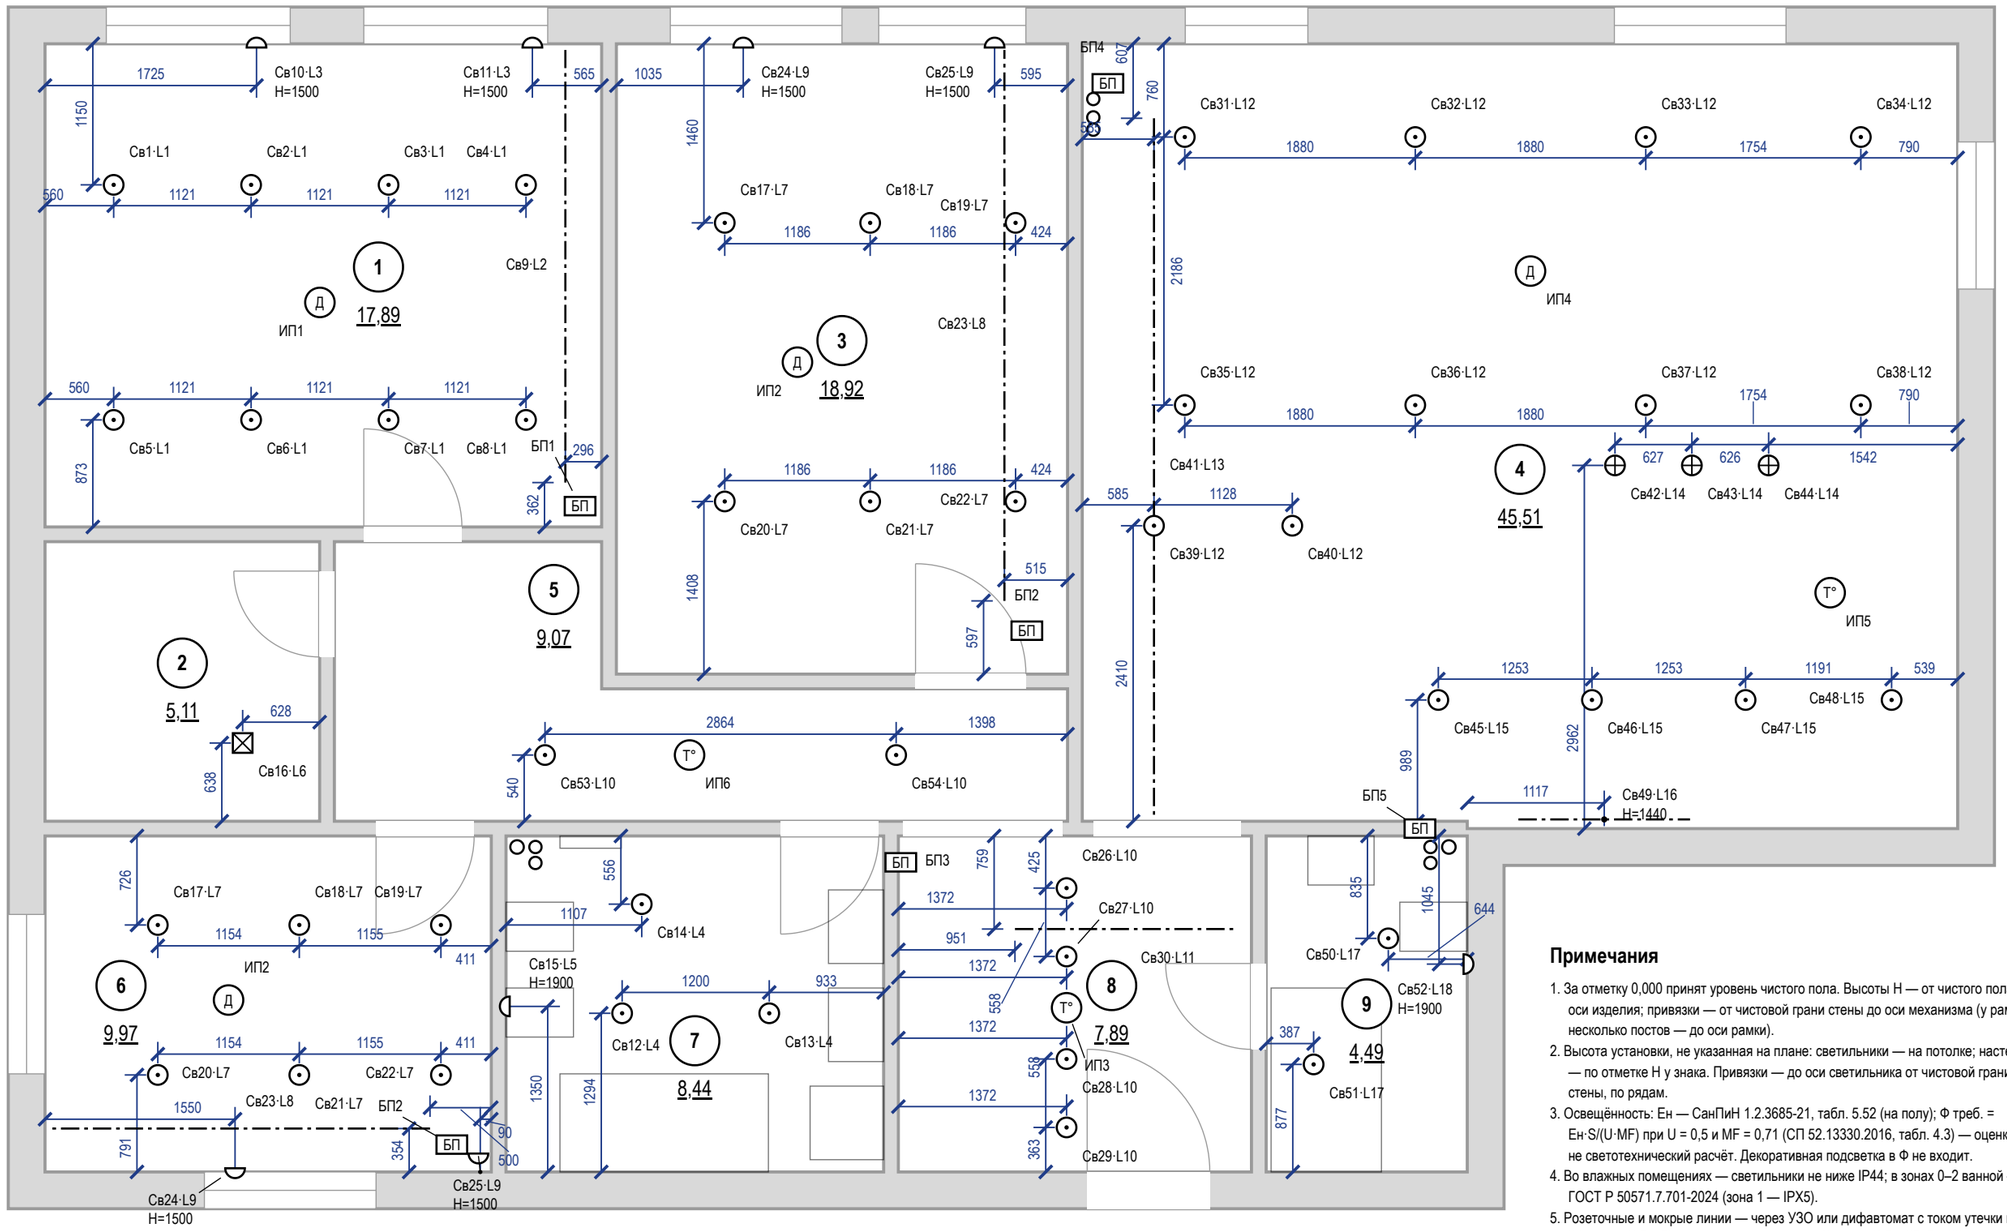

Примечания

1. За отметку 0,000 принят уровень чистого пола. Высоты H — от чистого пола до оси изделия; привязки — от чистовой грани стены до оси механизма (у рамки на несколько постов — до оси рамки).
2. Высота установки, не указанная на плане: светильники — на потолке; настенные — по отметке H у знака. Привязки — до оси светильника от чистовой грани стены, по рядам.
3. Освещённость: Eн — СанПиН 1.2.3685-21, табл. 5.52 (на полу); Ф треб. = Eн·S/(U·MF) при U = 0,5 и MF = 0,71 (СП 52.13330.2016, табл. 4.3) — оценка, не светотехнический расчёт. Декоративная подсветка в Ф не входит.
4. Во влажных помещениях — светильники не ниже IP44; в зонах 0–2 ванной — по ГОСТ Р 50571.7.701-2024 (зона 1 — IPX5).
5. Розеточные и мокрые линии — через УЗО или дифавтомат с током утечки не более 30 мА (ПУЭ 7.1.79); в санузле выполнить ДСУП (ПУЭ 7.1.87–7.1.88).
6. Кабель — медный, исполнение нг(A)-LS (ГОСТ 31565-2012); скрытая прокладка только горизонтально и вертикально, фактические трассы зафиксировать исполнительной схемой до закрытия отделкой.
7. Расчёт нагрузок, токов КЗ, селективности и сечений — по проекту ЭОМ организации с допуском СРО; лист задаёт состав, расположение и группы.
8. Ведомость светильников — лист «Ведомость электроточек и изделий».

					Проект: Квартира с кабинетом
	Лист	№ док.	Подпись	Дата	
Дизайнер	Кырлан А.С.			21.10.26	План освещения

Стадия	Лист	Листов
П	24	97

выпуск 18.10.2026 № 918b20bf25 · стр. 24 из 97

Спецификация светильников

Поз.	Марки	Наименование	Установка	Кол.	P, Вт	Σ P, Вт	Ф, лм	Тц, К	Ra	Угол, °	IP	Дим.	Группа	Пом.
1	Св1–Св8	Встраиваемый точечный	встраиваемый	8	12	96	1000	2700	90	—	20	—	L1	1
2	Св9	Лента светодиодная 24 В	в коробе, профиль с рассеивателем	15,5 м	9,6/м	148,8	900/м	2700	90	—	20	да	L2	1
3	Св10, Св11, Св24, Св25	Настенный (бра)	на стене, H=1500	6	6	36	400	2700	90	60	20	—	L3, L9	1, 3, 6
4	Св16	Потолочный накладной	на потолке, засветка стены	1	10	10	900	3000	90	—	20	—	L6	2
5	Св17–Св22	Встраиваемый точечный	встраиваемый	12	12	144	1050	2700	90	—	20	—	L7	3, 6
6	Св23	Лента светодиодная 24 В	в коробе, профиль с рассеивателем	24,6 м	9,6/м	236,2	900/м	2700	90	—	20	да	L8	3, 6
7	Св31–Св40	Встраиваемый точечный	встраиваемый	10	12	120	1000	3000	90	—	20	да	L12	4
8	Св41	Лента светодиодная 24 В	в коробе, профиль с рассеивателем	22,1 м	9,6/м	212,2	900/м	2700	90	—	20	да	L13	4
9	Св42, Св43, Св44	Подвесной	подвес, низ H=1450	3	9	27	800	3000	90	—	20	да	L14	4
10	Св45–Св48	Встраиваемый точечный	встраиваемый	4	10	40	900	3000	90	—	20	да	L15	4
11	Св49	Линейный настенный	под верхними шкафами, H=1440	1	18	18	1500	3000	90	—	20	да	L16	4
12	Св26–Св29, Св53, Св54	Встраиваемый точечный	встраиваемый	6	7	42	600	3000	90	—	20	—	L10	5, 8
13	Св12–Св14, Св51	Встраиваемый точечный	встраиваемый	4	6	24	500	3000	90	—	44	—	L4, L17	7, 9
14	Св15, Св52	Настенный светильник над зеркалом, драйвер встроен	над зеркалом, H=1900	2	8	16	600	3000	90	—	44	—	L5, L18	7, 9
15	Св30	Лента светодиодная 24 В	в коробе, профиль с рассеивателем, датчик движения	1,8 м	4,8/м	8,6	150/м	2700	90	—	20	нет	L11	8
16	Св50	Встраиваемый точечный	встраиваемый	1	7	7	600	3000	90	—	44	—	L17	9
		Итого		**58 шт + 64 м**		**1185,8**								

Слои света по помещениям

Пом.	Помещение	Слои света и группы включения (марки светильников)	Тц, К	Ra	Σ P, Вт	Сцен.
1	Спальня	общий — L1 (Св1–Св8); рабочий — L3 (Св10, Св11); акцентный — L2 (Св9)	2700	90	256,8	2
2	Гардеробная-постирочная	общий — L6 (Св16)	3000	90	10	—
3	Кабинет	общий — L7 (Св17–Св22); рабочий — L9 (Св24, Св25); акцентный — L8 (Св23)	2700	90	202,1	1
4	Кухня-гостиная	общий — L12 (Св31–Св40), L14 (Св42, Св43, Св44), L15 (Св45–Св48); рабочий — L16 (Св49); акцентный — L13 (Св41)	2700 / 3000	90	417,2	4
5	Коридор	общий — L10 (Св53, Св54)	3000	90	14	—
6	Детская	общий — L7 (Св17–Св22); рабочий — L9 (Св24, Св25); акцентный — L8 (Св23)	2700	90	202,1	1
7	Ванная	общий — L4 (Св12–Св14); рабочий — L5 (Св15)	3000	90	26	—
8	Прихожая	общий — L10 (Св26–Св29); ночной — L11 (Св30)	2700 / 3000	90	36,6	—
9	Санузел гостевой	общий — L17 (Св50, Св51); рабочий — L18 (Св52)	3000	90	21	—

LED-ленты, линейные светильники и блоки питания

Марка	Пом.	L, м	U, В	Вт/м	Σ P, Вт	БП	P БП, Вт	Загр., %	Питание	Доступ к БП
Св9	1	15,5	24	9,6	148,8	БП1	200	74	с двух концов	люк 300×300 в коробе У1 у входа
Св23	3	12,3	24	9,6	118,1	БП2	200	59	с двух концов	люк 300×300 в коробе У1 у окна
Св41	4	22,1	24	9,6	212,2	БП4	300	71	с двух концов	люк 300×300 в коробе У1 у входа
Св49	4	3	24	—	18	БП5	60	30	встроенный ввод	в пенале М6, верх, съёмная панель
Св23	6	12,3	24	9,6	118,1	БП2	200	59	с двух концов	люк 300×300 в коробе У1 у окна
Св30	8	1,8	24	4,8	8,6	БП3	20	43	с одного конца	в шкафу М16, верхняя полка

Сценарии освещения

Пом.	Сценарий	Группы и уровни, %	Чем включается
1	Вечер	L1 споты — 0; L2 подсветка короба — 100; L3 бра — 100	S1, S2, S3
1	Уборка	L1 споты — 100; L2 подсветка короба — 100; L3 бра — 0	S1, S2, S3
3	Вечер	L7 споты — 0; L8 подсветка короба — 100; L9 бра — 100	S4, S5, S6
4	Вечер	L12 споты гостиной — 30; L13 подсветка короба — 100; L14 подвесы над столом — 50; L15 споты кухни — 0; L16 подсветка столешницы — 0	S10 светорегулятор, S11 светорегулятор
4	Ужин	L12 споты гостиной — 0; L13 подсветка короба — 60; L14 подвесы над столом — 100; L15 споты кухни — 0; L16 подсветка столешницы — 30	S10 светорегулятор, S11 светорегулятор, S12 светорегулятор
4	Кино	L12 споты гостиной — 0; L13 подсветка короба — 20; L14 подвесы над столом — 0; L15 споты кухни — 0; L16 подсветка столешницы — 0	S10 светорегулятор
4	Готовка	L12 споты гостиной — 50; L13 подсветка короба — 0; L14 подвесы над столом — 0; L15 споты кухни — 100; L16 подсветка столешницы — 100	S10 светорегулятор, S11 светорегулятор, S12 светорегулятор
6	Вечер	L7 споты — 0; L8 подсветка короба — 100; L9 бра — 100	S4, S5, S6

Слои света

общий — равномерный свет помещения, по норме освещённости

рабочий — местный свет задачи: столешница, зеркало, чтение у кровати

акцентный — подсветка потолка, стен и ниш; не входит в поток общего света


ночной — путь спальня → санузел: не выше 2700 K, малая яркость, датчик движения

Примечания

1. Позиции и марки Св — те же, что на плане освещения (лист 24) и в ведомости светильников (лист «Ведомость электроточек и изделий»); группы L — по плану выключателей (лист 26).
2. Модели светильников не назначены: подбор по графам спецификации — поток, Тц, Ra, угол, IP и диммирование не хуже указанных, мощность не больше. IP 20 — сухие помещения.
3. Длина LED-ленты в карнизе — по линии карниза плана потолков (лист 21); Σ P = Вт/м × длина. Блок питания загружен не больше чем на 80 %; лента 24 В длиннее 10 м питается с двух концов; доступ к блоку питания — люк ревизии 300×300 мм или место, указанное в таблице.
4. Сценарии: уровень — доля максимальной яркости группы, %; 0 — группа выключена. Уровень ниже 100 % — только у групп на светорегуляторе (задний фронт, TE) с диммируемыми драйверами и блоками питания.
5. Мощность и поток — по паспортам принятых изделий, Σ P — установленная мощность освещения. Оценка освещённости — на плане освещения; это не светотехнический расчёт.

					Проект: Квартира с кабинетом
	Лист	№ док.	Подпись	Дата	Спецификация светильников и сценарии освещения
Дизайнер	Кырлан А.С.			21.10.26	Стадия: П; Лист: 25; Листов: 97

Правка к этому листу

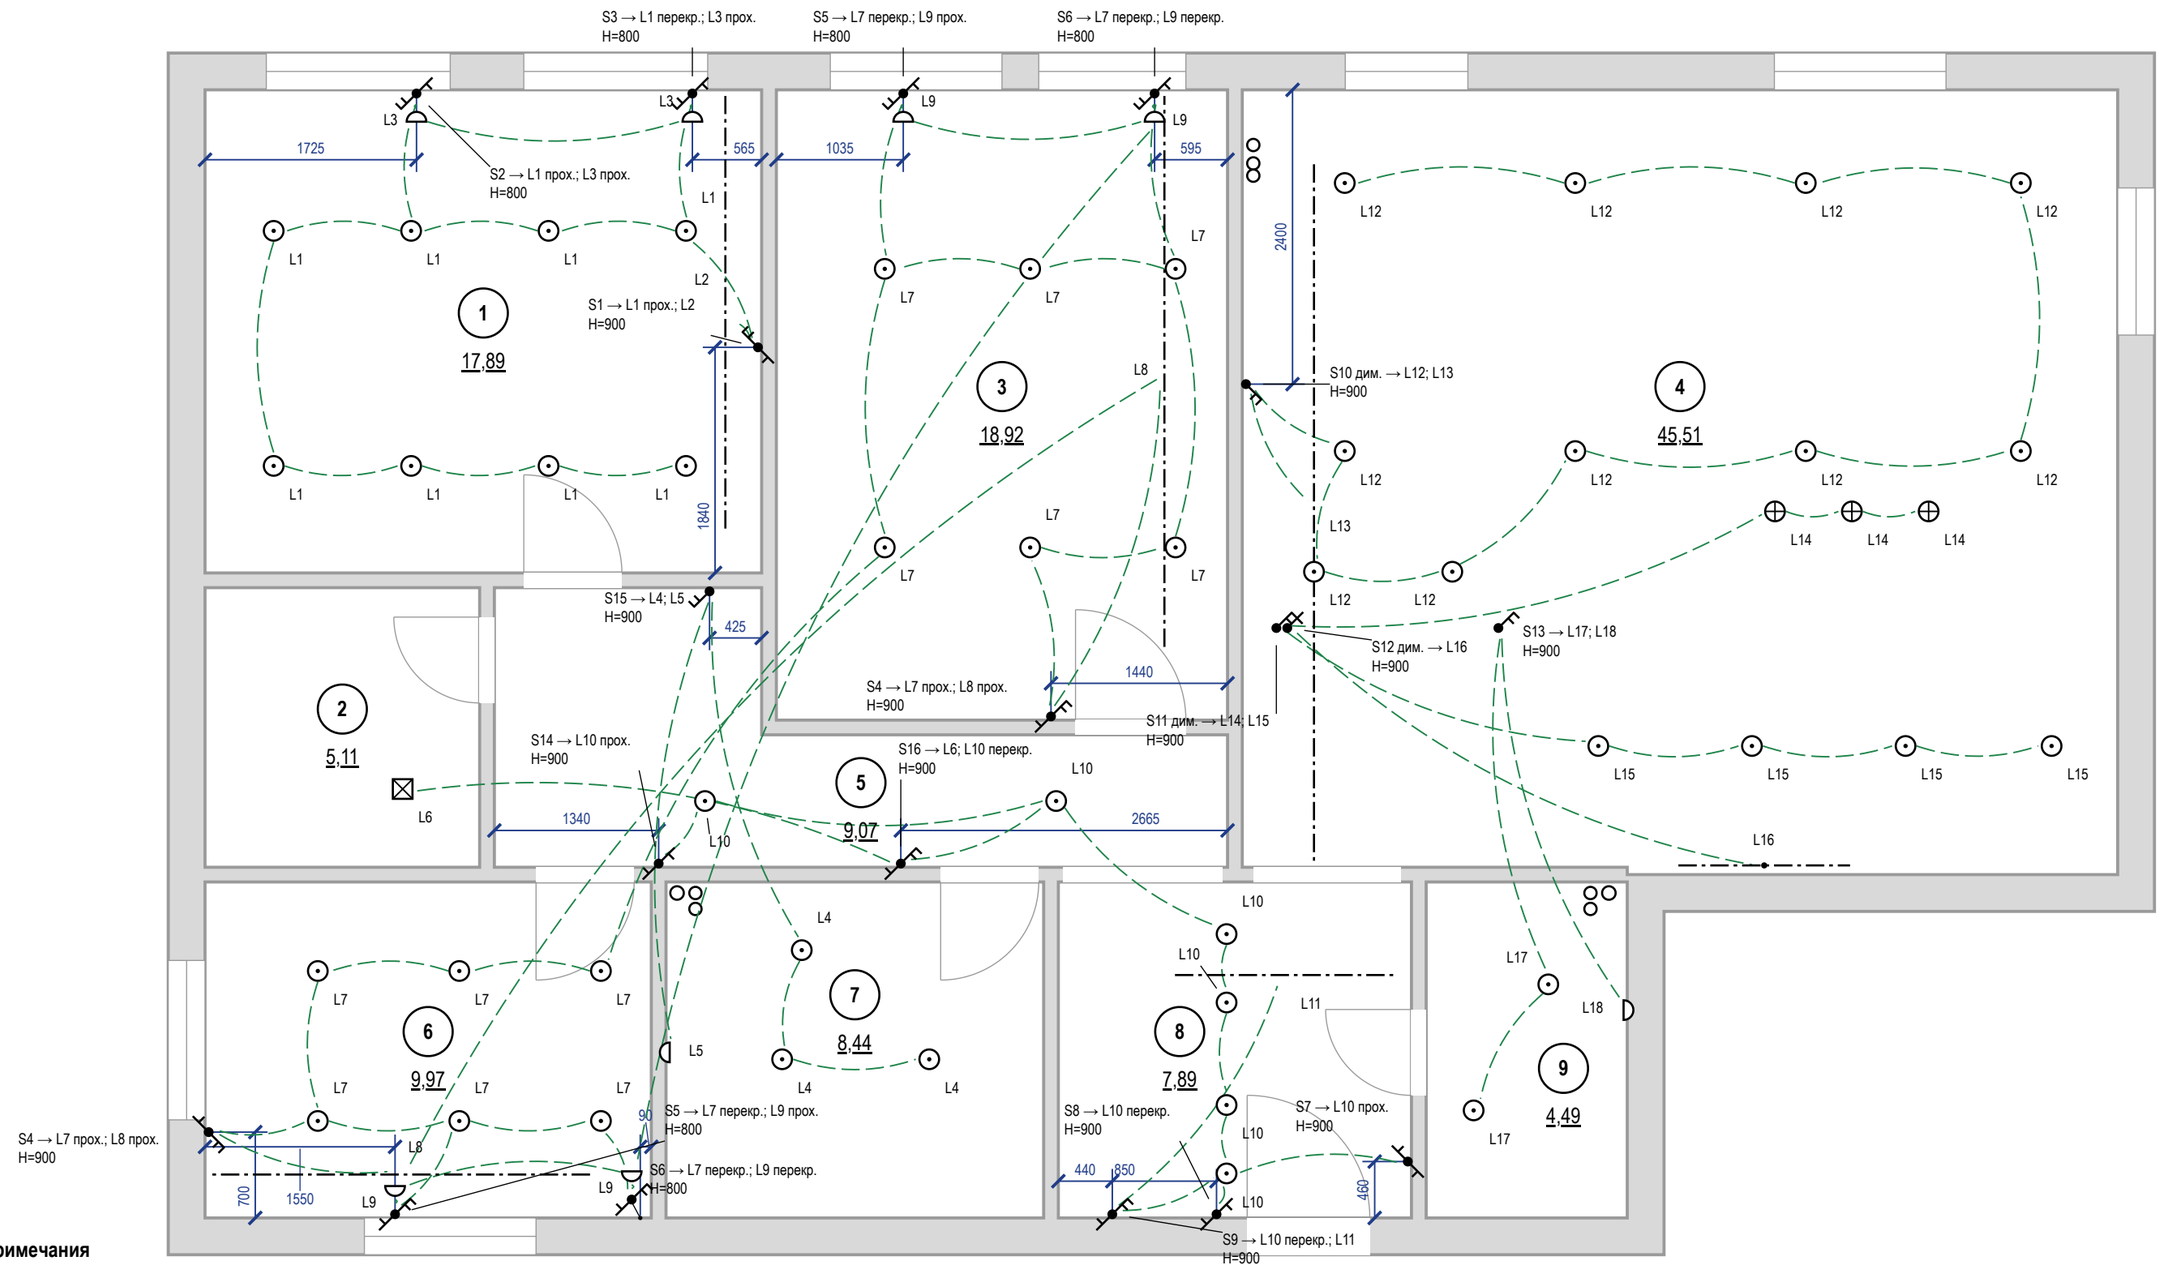

Примечания


1. За отметку 0,000 принят уровень чистого пола. Высоты H — от чистого пола до оси изделия; привязки — от чистовой грани стены до оси механизма (у рамки на несколько постов — до оси рамки).
2. Высота установки, не указанная на плане: выключатели — 900 мм от чистого пола, со стороны дверной ручки (ПУЭ 7.1.51).
3. Линии связи показывают, какой выключатель какую группу L включает; это не трасса кабеля. Трасса — принципиальная, фактическую зафиксировать исполнительной схемой.
4. Группы из нескольких мест (L1 — S1, S2, S3; L3 — S2, S3; L7 — S4, S4, S5, S5, S6, S6; L8 — S4, S4; L9 — S5, S5, S6, S6; L10 — S7, S8, S9, S14, S16): на крайних местах — проходные клавиши, на промежуточных — перекрёстные; механизмы — в ведомости изделий.
5. Светорегулятор — по заднему фронту (для LED-драйверов), совместимость с драйверами проверить до закупки.
6. Розеточные и мокрые линии — через УЗО или дифавтомат с током утечки не более 30 мА (ПУЭ 7.1.79); в санузле выполнить ДСУП (ПУЭ 7.1.87–7.1.88).
7. Кабель — медный, исполнение нг(A)-LS (ГОСТ 31565-2012); скрытая прокладка только горизонтально и вертикально, фактические трассы зафиксировать исполнительной схемой до закрытия отделкой.
8. Расчёт нагрузок, токов КЗ, селективности и сечений — по проекту ЭОМ организации с допуском СРО; лист задаёт состав, расположение и группы.
9. Расшифровка клавиш и ведомость изделий — лист «Ведомость электроточек и изделий».

					Проект: Квартира с кабинетом
	Лист	№ док.	Подпись	Дата	Управление светильниками
Дизайнер	Кырлан А.С.			21.10.26	

Стадия	Лист	Листов
П	26	97

выпуск 18.10.2026 № 918b20bf25 · стр. 26 из 97

Правка к этому листу

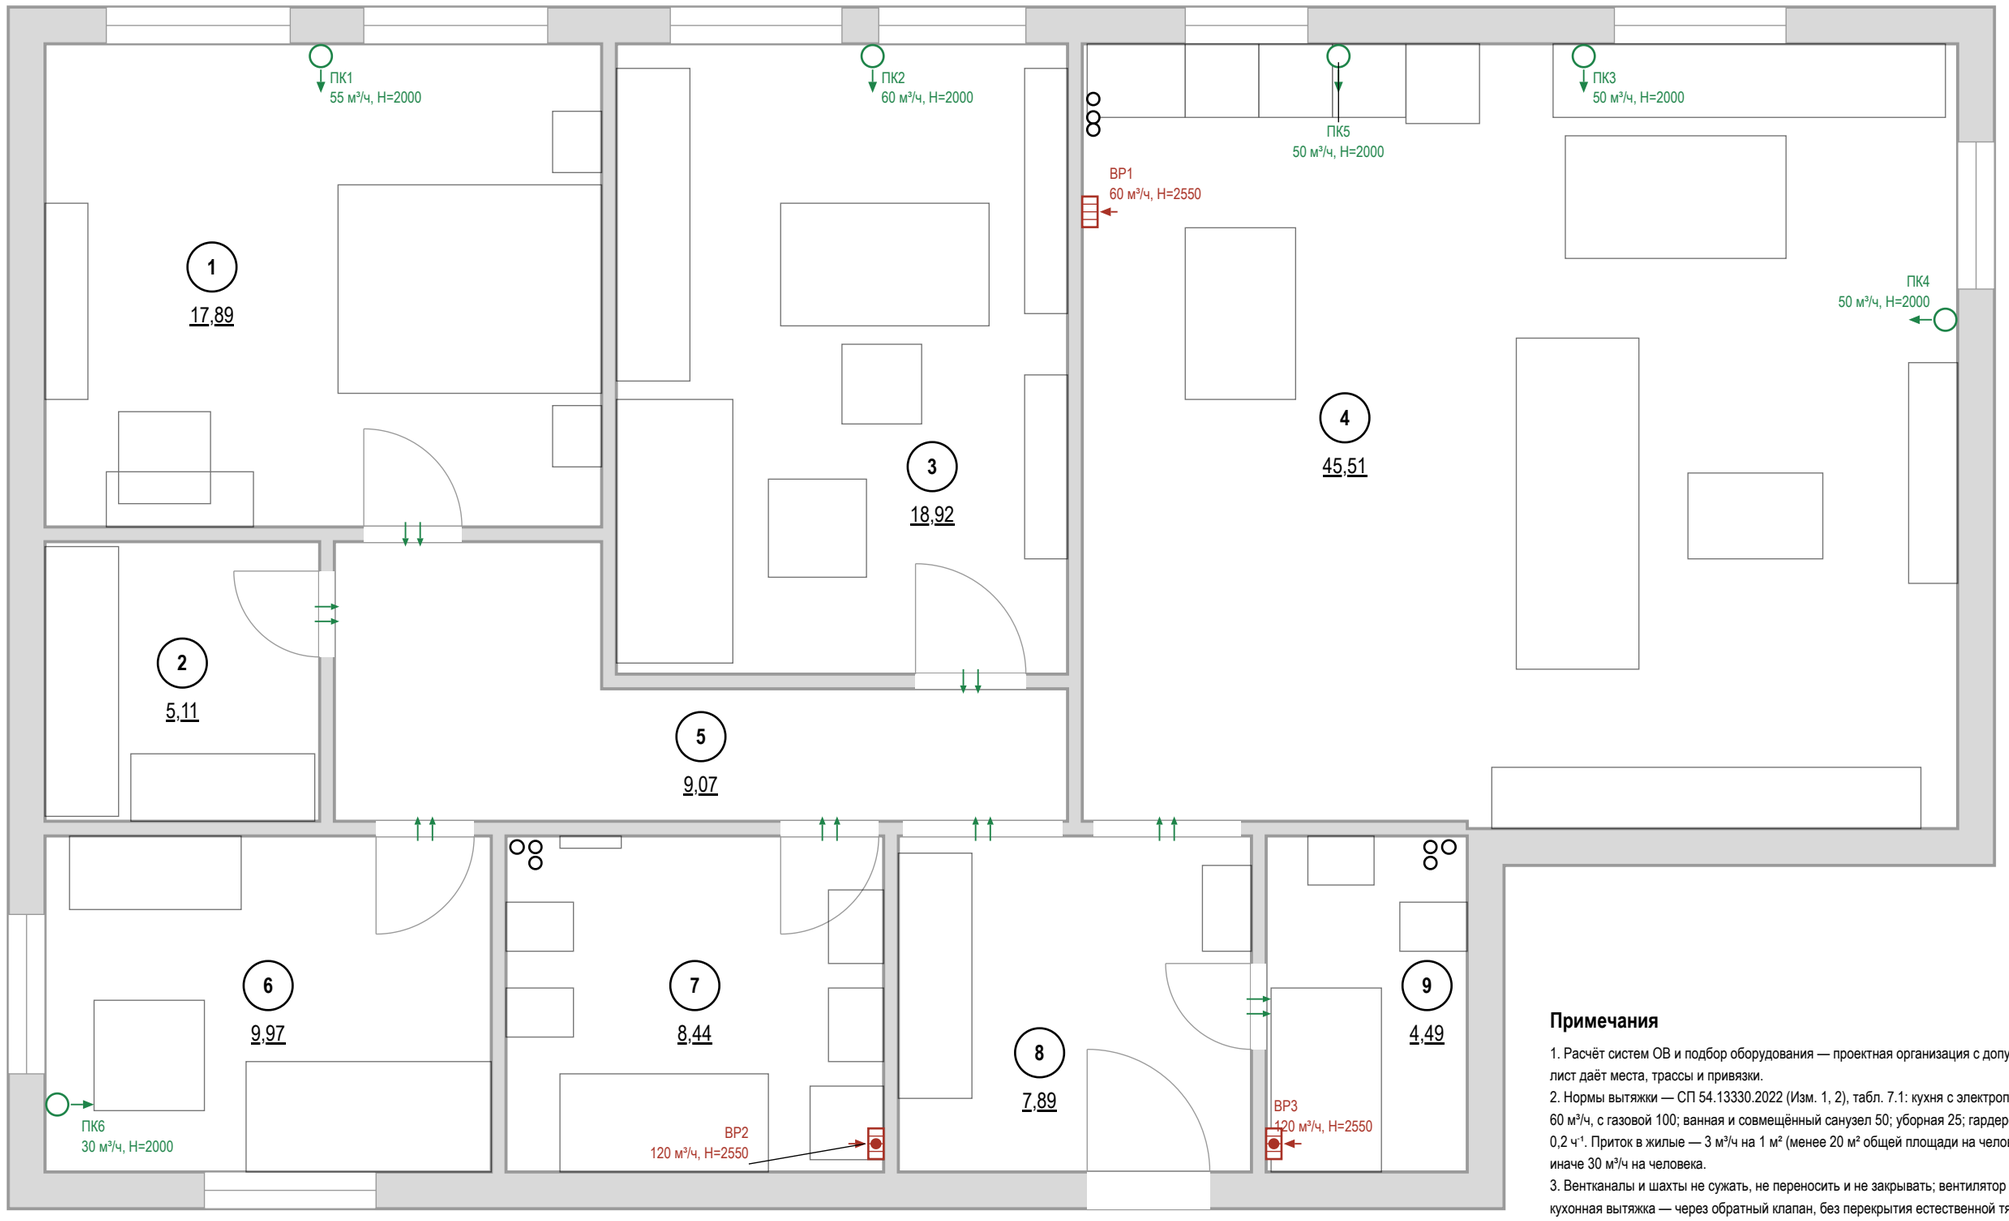

Примечания


1. Расчёт систем ОВ и подбор оборудования — проектная организация с допуском СРО; лист даёт места, трассы и привязки.
2. Нормы вытяжки — СП 54.13330.2022 (Изм. 1, 2), табл. 7.1: кухня с электроплитой 60 м³/ч, с газовой 100; ванная и совмещённый санузел 50; уборная 25; гардеробная 0,2 ч⁻¹. Приток в жилые — 3 м³/ч на 1 м² (менее 20 м² общей площади на человека), иначе 30 м³/ч на человека.
3. Вентканалы и шахты не сужать, не переносить и не закрывать; вентилятор и кухонная вытяжка — через обратный клапан, без перекрытия естественной тяги.
4. Проектные расходы — не ниже нормы, вытяжка сведена с притоком вентиляторами мокрых помещений. Клапаны — в простенке у окна, центр 2000 мм, не над кроватью, не ближе 300 мм к стоякам отопления; типоразмер — на расход.
5. Переток — зазор под полотнами межкомнатных дверей или переточная решётка.
6. Кондиционирование заданием не предусмотрено; при установке трассы фреона и дренажа (не менее 40 мм/м, в К1 через сифон) и питание заложить до черновых работ.
7. Привязки оборудования — по паспортам приобретённых моделей, до черновых работ.

					Проект: Квартира с кабинетом
	Лист	№ док.	Подпись	Дата	
Дизайнер	Кырлан А.С.			21.10.26	План вентиляции

Стадия	Лист	Листов
П	27	97

выпуск 18.10.2026 № 918b20bf25 · стр. 27 из 97


Правка к этому листу

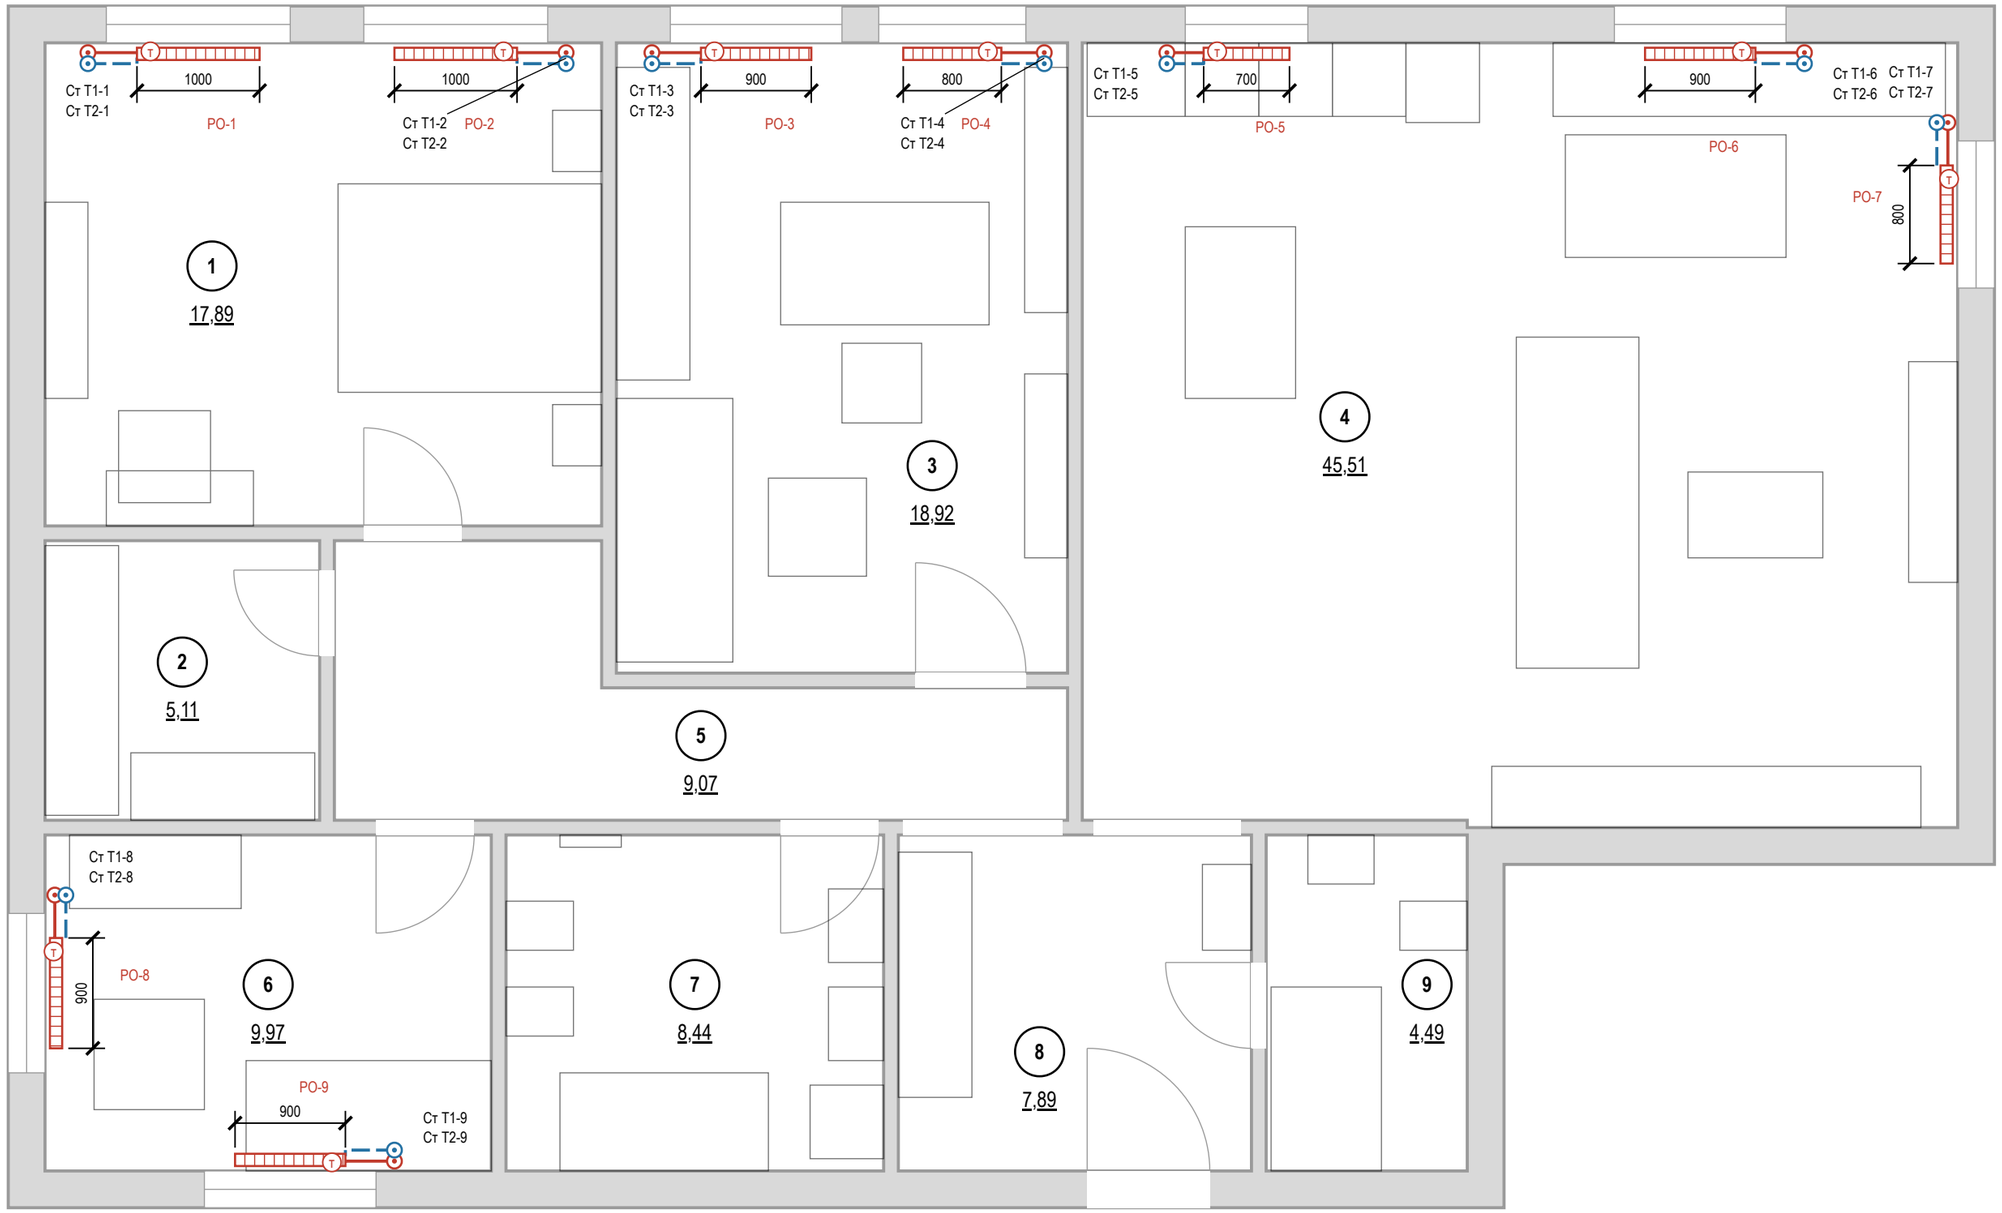




Примечания

1. Расчёт системы отопления, теплопотерь и подбор приборов — проектная организация с допуском СРО; лист даёт места и привязки.
2. Тип, длина и мощность радиаторов — по теплотехническому расчёту; лист задаёт места, зазоры и подключение.
3. Радиаторы — под каждым окном жилых комнат и кухни, центр по оси проёма, длина 0,7 ширины окна (кратно 100); окончательно — по расчёту.
4. Зазоры радиатора: низ не менее 100 мм от чистого пола, верх не менее 100 мм до подоконника, 30–50 мм от стены до задней панели; центр по оси окна с допуском ±20 мм.
5. Радиаторы не закрывать глухими коробами и мебелью; перенос и замена приборов в многоквартирном доме — переустройство, согласование с управляющей организацией (ЖК РФ ст. 25–26); вынос на лоджию запрещён.
6. Трубы отопления через межквартирные стены не прокладывать (СП 51.13330.2011, п. 9.19); через перекрытия и перегородки — в гильзах.
7. Привязки приборов и подводок — по паспортам приобретённых радиаторов и клапанов, до черновых работ.
8. До закрытия отделкой трубопроводы отопления испытать гидростатическим давлением с оформлением акта (СП 73.13330.2016, 7.2–7.3).

					Проект: Квартира с кабинетом
	Лист	№ док.	Подпись	Дата	План отопления
Дизайнер	Кырлан А.С.			21.10.26	Стадия: П; Лист: 28; Листов: 97

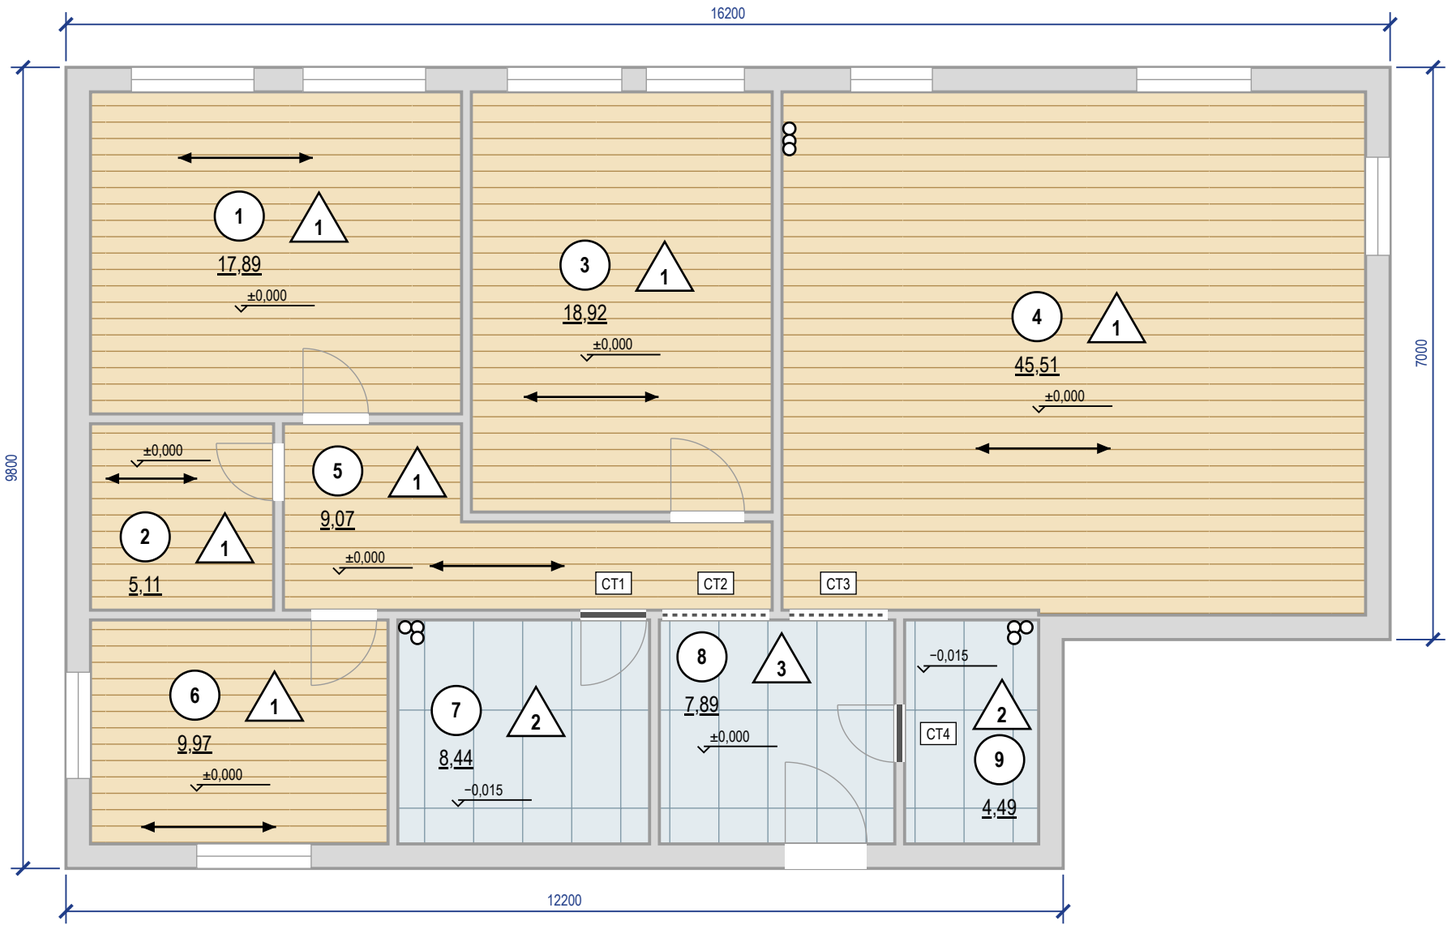

Экспликация полов

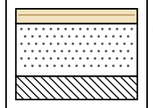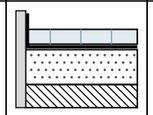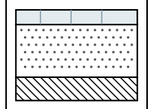Номер помещения	Тип пола	Схема пола	Данные элементов пола (наименование, толщина, основание), мм	Площадь, м²
1, 2, 3, 4, 5, 6	1		Инженерная доска на клею — 14 Стяжка ЦПС М200 — 50 Плита перекрытия Всего 64 мм; ЧП ±0,000, верх плиты −0,064	106,47
7, 9	2		Керамогранит на клею С2 TE S1 — 14 Гидроизоляция обмазочная, 2 слоя, с заведением на стены 200 мм — 2 Стяжка ЦПС М200 — 33 Плита перекрытия Всего 49 мм; ЧП −0,015, верх плиты −0,064	12,93
8	3		Керамогранит на клею С2 TE S1 — 14 Стяжка ЦПС М200 — 50 Плита перекрытия Всего 64 мм; ЧП ±0,000, верх плиты −0,064	7,89
			Итого	**127,29**

Спецификация плинтусов

Наименование	Помещения	Длина, м (с запасом)
Плинтус МДФ под покраску 80×16, крепление к стене, окраска в цвет Farrow & Ball No. 15	1, 2, 3, 4, 5, 8	94
SX165, h = 69 мм, крепление к стене, окраска в цвет Farrow & Ball No. 15	6	14

Отметки по высоте

±0,000	чистый пол пом. 1–6, 8; отсчёт высот
−0,015	чистый пол пом. 7, 9, ниже на 15 мм
−0,064	верх плиты — расчёт, не замер (задание на обмер)
сущ. пол	снимается до плиты; не замерен (задание на обмер)

Примечания

1. За отметку ±0,000 принят чистый пол, не существующий (блок отметок). Площади — по чистым размерам помещений, м²; размеры — в мм.
2. Стык разнотипных покрытий — по оси дверного полотна (под полотном в закрытом положении); решение стыка — по ведомости стыков.
3. Пол санузлов ниже смежных помещений на 15 мм за счёт меньшей толщины стяжки (верх плиты общий — по экспликации полов); гидроизоляция по стяжке с заведением на стены не менее 200 мм (СП 29.13330.2011, п. 7.2), до облицовки — тест проливом и акт скрытых работ.
4. Трубопроводы в конструкции пола не прокладываются: пирог пола 49–64 мм не вмещает выпуски канализации с уклоном — выпуски К1 ведутся по стенам над чистым полом в коробах (лист 16).
5. Звукоизоляционный слой под стяжкой проектом не предусмотрен (стяжка по плите): приведённый уровень ударного шума перекрытия с полом Lnw не более 60 дБ (СП 51.13330.2011, табл. 2) подтвердить по данным дома; при превышении — плавающая стяжка по звукоизоляции с демпферной лентой по контуру и у стояков, пирог пересчитать.
6. Штучные покрытия (инженерная доска): направление — по стрелке; влажность основания по СМ не более 2,0 % (по ТУ изготовителя).
7. Ровность основания — просвет под 2-метровой рейкой не более 2 мм: пом. 1, 2, 3, 4, 5, 6 (инженерная доска), пом. 7, 8, 9 (керамогранит); проверить до укладки покрытия (СП 71.13330.2017, табл. 8.5).
8. Сетка на плитке — условная, в размер формата; точка старта и раскладка — по листу раскладки плитки.
9. Пироги полов — по экспликации полов: слои сверху вниз, толщины в мм; гидроизоляция мокрых зон — в пироге и в ведомости отделки; схема пола — без масштаба.


					Проект: Квартира с кабинетом
	Лист	№ док.	Подпись	Дата	
Дизайнер	Кырлан А.С.			21.10.26	План покрытий пола

Стадия	Лист	Листов
П	29	97


выпуск 18.10.2026 № 918b20bf25 · стр. 29 из 97

Правка к этому листу

Фрагмент 1. Ванная (пом. 7). Пол 600×600, шов 2 мм, М 1:25

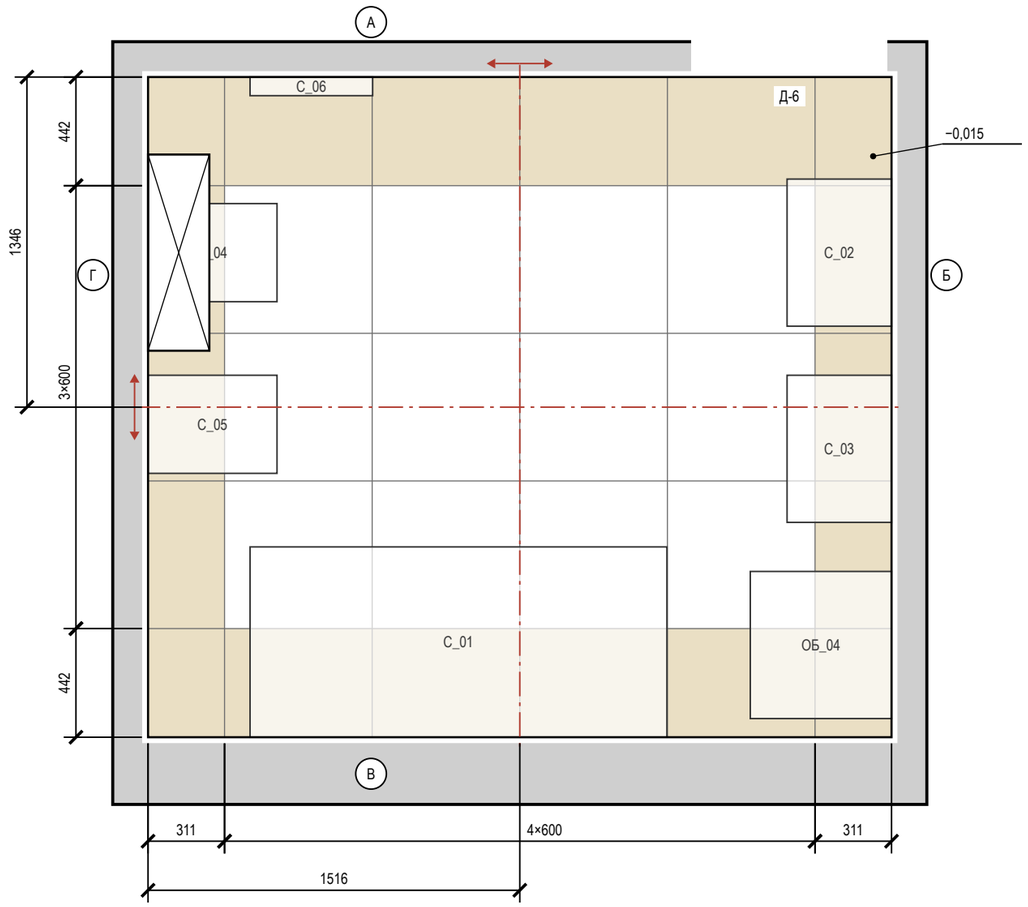

Фрагмент 2. Санузел гостевой (пом. 9). Пол 600×600, шов 2 мм, М 1:25

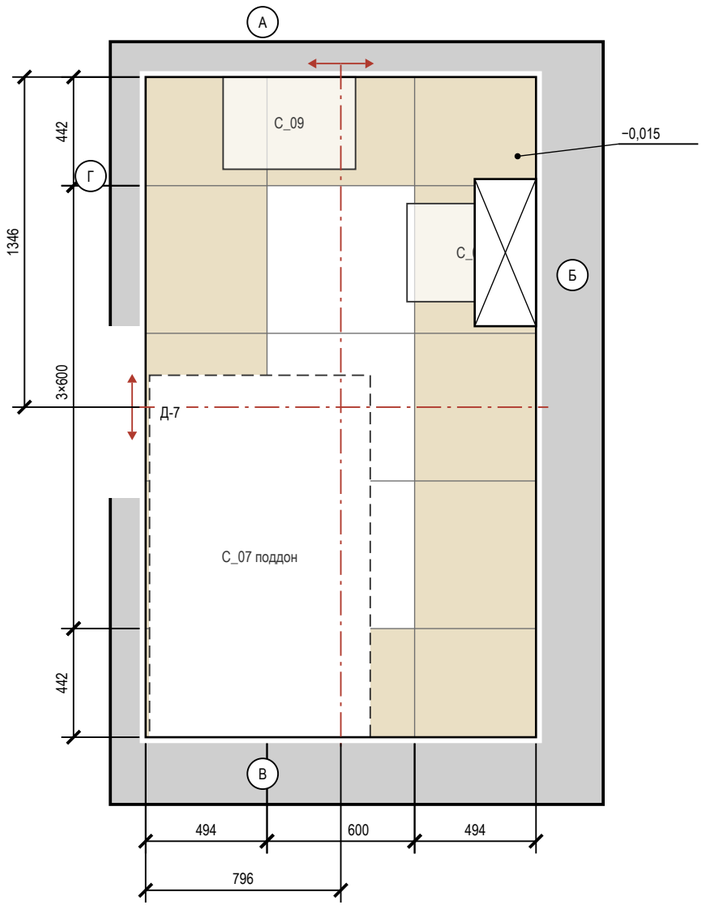

Примечания

1. Раскладка от чистовых размеров: стены санузлов теряют 10 + 5 + 9 = 24 мм на сторону (штукатурка, клей, плитка); подрезки чистые, без шва.
2. Старт — от центра помещения (штрихпунктир, стрелки направление укладки); размер старта — от чистовых стен Г и А.
3. Раскладка пола «Прихожая» и фартука «Кухня-гостиная» — на листе «Раскладка плитки. Прихожая. Фартук кухни».
4. Калибр партии не задан — до укладки замерить (рабочий размер W, ГОСТ 13996-2019) и пересчитать подрезки.
5. Количество: целые по раскладке + по одной на подрезку, запас 10 %; один артикул — одна партия и тон. Исключены поддон, короб, проёмы и места за коробом; S — по чистым граням: стены нетто = зона облицовки по ведомости отделки − место за коробом инсталляции 1,68 м² (плитку за коробом не кладут), короб отдельной строкой.
6. Клей C2 TE S1 Ceresit CM 17; C2 TE S1 (ГОСТ Р 56387-2018), затирка CG2WA Mapei Ultracolor Plus 132; CG2WA; расход — по ТУ выбранной марки.
7. Гидроизоляция: пол и стены 200 мм от ЧП; над ванной — до 2000 и 300 мм за борт, у душа — до 2000 и 500 мм за поддон (см. развёртки); акт скрытых работ, пролив 24 ч.
8. Швы пола совмещены со швами стены А; по периметру — демпферная лента.
9. Отметка чистого пола −0,015, порог 15 мм; стык с соседним покрытием — по оси полотна двери.

Ведомость плитки

Помещение, поверхность	Плитка, код	Формат	Шов	S, м²	Целых	Подр.	С запасом
Ванная, пол	аналог: керамогранит под травертин	600×600	2	8,44	12	18	33
Ванная, стены А–Г	аналог: керамогранит под травертин	600×1200	2	25,34	24	19	49
Ванная, короб инсталляции	аналог: керамогранит под травертин	600×1200	2	1,76	0	6	7
Санузел гостевой, пол	аналог: керамогранит под травертин	600×600	2	4,49	1	14	17
Санузел гостевой, стены А–Г	аналог: керамогранит под травертин	600×1200	2	18,87	9	22	35
Санузел гостевой, короб инсталляции	аналог: керамогранит под травертин	600×1200	2	1,47	1	3	5
Прихожая, пол	A8UZ	600×1200	2	7,89	3	12	17
Кухня-гостиная, фартук (ст. А)	аналог: керамогранит под травертин, матовый	1200×600	2	0,70	0	2	3
Итого 600×600				12,93	13	32	50
Итого 600×1200				**56,03**	**37**	**64**	**116**

Ведомость материалов

Материал	Класс, код	Норма расхода	Кол-во
Затирка	CG2WA Mapei Ultracolor Plus 132	(a+b)/ab·шов·t·1,6	4,8 кг
Затирка	CG2WA	(a+b)/ab·шов·t·1,6	0,7 кг
Клей	C2 TE S1 Ceresit CM 17	1,5 кг/м²·мм, слой 5	473 кг (19 меш.)
Клей	C2 TE S1	1,5 кг/м²·мм, слой 5	70 кг (3 меш.)
Гидроизоляция	обмазочная, 2 слоя: пол, стены по периметру и зоны замачивания	по ТУ	28,2 м²
Демпф. лента	по периметру пола из плитки		28,0 м

Условные обозначения

- плитка целая; тонкая линия — шов
- плитка с подрезкой (размер — на цепочке)
- ось старта; стрелки — направление укладки
- сантехприбор: габарит, высота по практике
- поддон душа — плитку пола под ним не кладут
- короб инсталляции: плитка пола — до короба
- отметка чистого пола на полке выноски, м
- (А) обозначение стены А–Г (как на развёртках)


					Проект: Квартира с кабинетом
	Лист	№ док.	Подпись	Дата	Раскладка плитки. Планы полов
Дизайнер	Кырлан А.С.			21.10.26	

Стадия	Лист	Листов
П	30	97


выпуск 18.10.2026 № 918b20bf25 · стр. 30 из 97

Правка к этому листу

Фрагмент 1. Прихожая (пом. 8). Пол 600×1200, шов 2 мм, М 1:20

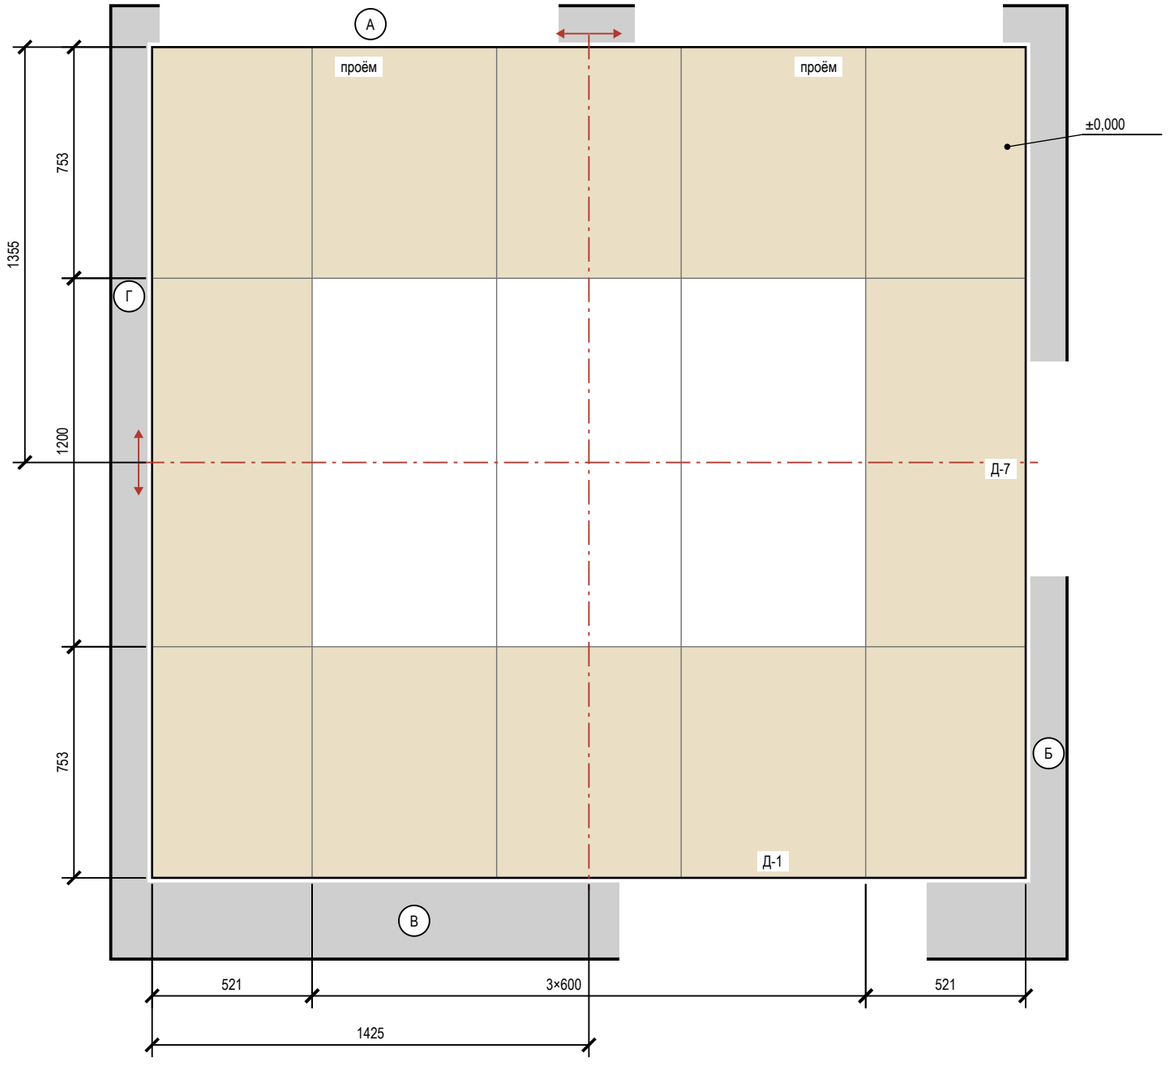

Фрагмент 2. Кухня-гостиная (пом. 4), фартук, стена А. 1200×600, шов 2 мм, М 1:20

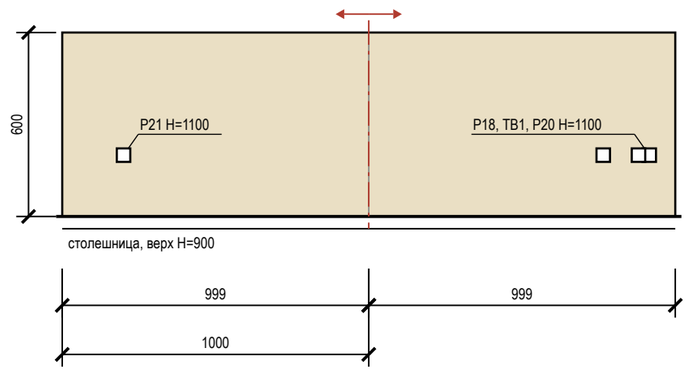

Условные обозначения

- плитка целая; тонкая линия — шов
- плитка с подрезкой (размер — на цепочке)
- ось старта; стрелки — направление укладки
- электроточка: марка и H — по листам ЭОМ
- столешница (верх)
- навесной шкаф над фартуком
- отметка чистого пола на полке выноски, м
- А — обозначение стены А–Г (как на развёртках)

Подсчёт плитки

Поверхность	Формат	S, м²	Целых	Подр.	С запасом
Прихожая, пол	600×1200	7,89	3	12	17
Кухня-гостиная, фартук (ст. А)	1200×600	0,70	0	2	3

Сдвиг розеток фартука под раскладку

Точка (ЭОМ)	Проект: от угла / H	Под раскладку: от угла / H	Сдвиг, мм
P18, TB1, P20	1765, 1915, 1880 / 1100	1765, 1915, 1880 / 1200	H +100 — ось ряда
P21	200 / 1100	200 / 1200	H +100 — ось ряда

Примечания

1. Прихожая: керамогранит 600×1200, длинная сторона — вдоль стен Б и Г, шов 2 мм, прямая раскладка от центра. Стены окрашены: раскладка от чистового контура минус штукатурка и шпаклёвка 15 мм на сторону (принято); подрезки 521 / 753 мм, срез — под плинтус.
2. Прихожая: деформационный зазор по периметру 8–10 мм под плинтусом; в проёмах — стык с соседним покрытием по оси полотна двери. Клей C2 TE S1, затирка CG2WA.
3. Фартук, Кухня-гостиная: 1200×600 горизонтально, шов 2 мм; зоны 2000 мм — 900…1500 (от столешницы до низа навесного шкафа, без шкафа — 600 мм). Старт от центра участка, подрезки 999 мм. Площадь 0,70 м² — как в ведомости отделки.
4. Фартук — после монтажа столешницы, низ на 2–3 мм выше неё, шов со столешницей — санитарный герметик; навесные шкафы — после фартука. Торцы у пенала и стены — профиль или запил 45°.
5. Розетки из таблицы переносятся до черновой электрики: по высоте — на ось ряда плитки, от вертикального шва крупной плитки — не ближе 60 мм. Привязка — от левого края фартука на развёртке.
6. Клей, затирка и итог по форматам — в ведомостях листа «Раскладка плитки. Планы полов».

					Проект: Квартира с кабинетом
	Лист	№ док.	Подпись	Дата	Раскладка плитки. Прихожая. Фартук кухни
Дизайнер	Кырлан А.С.			21.10.26	

Стадия	Лист	Листов
П	31	97

выпуск 18.10.2026 № 918b20bf25 · стр. 31 из 97

Правка к этому листу



					Проект: Квартира с кабинетом
	Лист	№ док.	Подпись	Дата	
Дизайнер	Кырлан А.С.			21.10.26	Визуализация. Вид сверху

Стадия	Лист	Листов
П	32	97

выпуск 18.10.2026 № 918b20bf25 · стр. 32 из 97

Правка к этому листу



					Проект: Квартира с кабинетом	
	Лист	№ док.	Подпись	Дата		
Дизайнер	Кырлан А.С.			21.10.26	Визуализация спальни	Стадия / Лист / Листов
						П / 33 / 97

выпуск 18.10.2026 № 918b20bf25 · стр. 33 из 97



					Проект: Квартира с кабинетом	
	Лист	№ док.	Подпись	Дата		
Дизайнер	Кырлан А.С.			21.10.26	Визуализация спальни	Стадия / Лист / Листов
						П / 34 / 97

выпуск 18.10.2026 № 918b20bf25 · стр. 34 из 97

Правка к этому листу



					Проект: Квартира с кабинетом	
	Лист	№ док.	Подпись	Дата		
Дизайнер	Кырлан А.С.			21.10.26	Визуализация спальни	Стадия / Лист / Листов
						П / 35 / 97

выпуск 18.10.2026 № 918b20bf25 · стр. 35 из 97

Правка к этому листу

Развёртка стены А


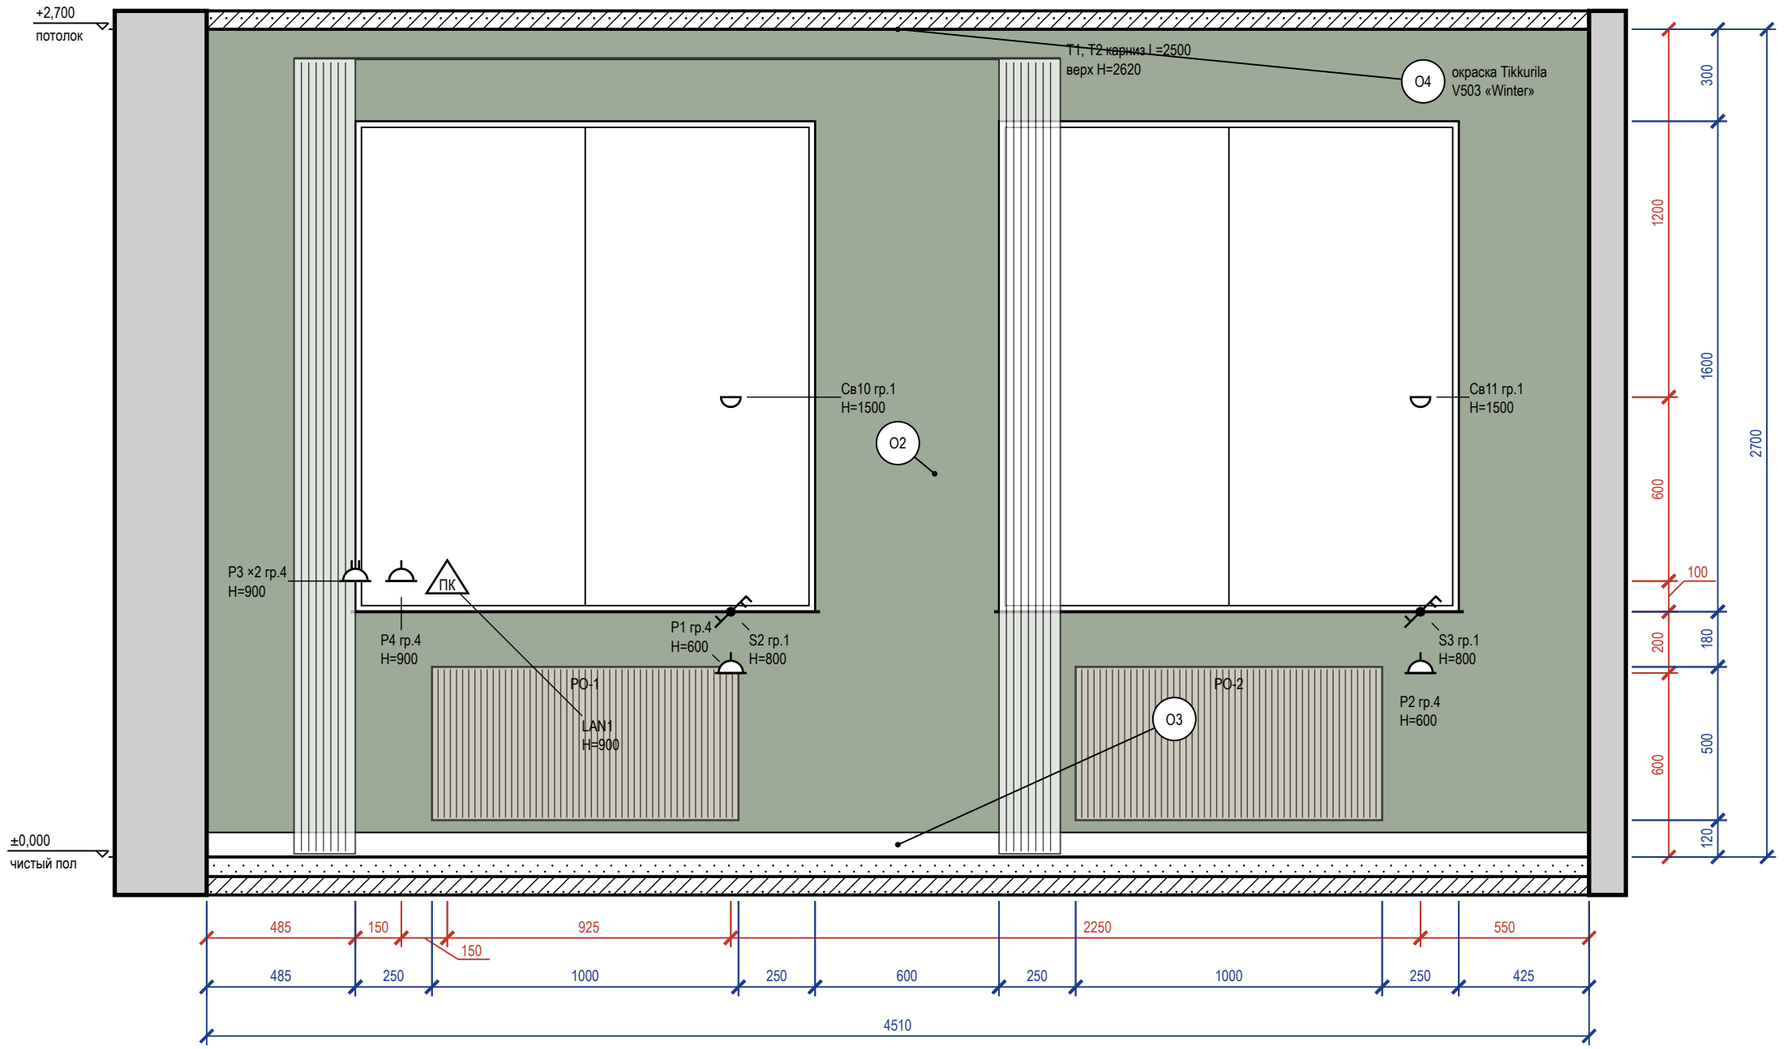


Схема развёрток (М 1:100)

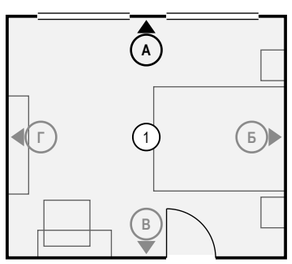

Ведомость отделки (на листе)

Марка	Поверхность	Материал, изделие	Цвет, код	Кол.
O2	акцентная стена	окраска, Farrow & Ball Modern Emulsion, матовая, подготовка Q3	Farrow & Ball No. 34 «Calke Green традиционный шалфей»	7,4 м²
O3	плинтус	плинтус МДФ, h 80 мм, аналог: плинтус МДФ под покраску 80×16	Farrow & Ball No. 15 «Bone — мягкий каменно-серый с зеленцой»	4,5 м
O4	потолок	окраска, Tikkurila Anti-Reflex 2, глубокоматовая, подготовка Q3	Tikkurila V503 «Winter»	17,9 м²

Визуализация этой стены — лист 33



Примечания

1. Размеры — в мм от чистовых поверхностей стен; условные обозначения и общие указания — лист 2.
2. Карнизы (шины) — по ведомости текстиля декоратора; длина L и верх H — по развёртке, крепление — до окраски потолка.

					Проект: Квартира с кабинетом
	Лист	№ док.	Подпись	Дата	Развёртка стены А. Спальня (пом. 1)
Дизайнер	Кырлан А.С.			21.10.26	

Стадия	Лист	Листов
П	36	97

выпуск 18.10.2026 № 918b20bf25 · стр. 36 из 97

Развёртка стены Б


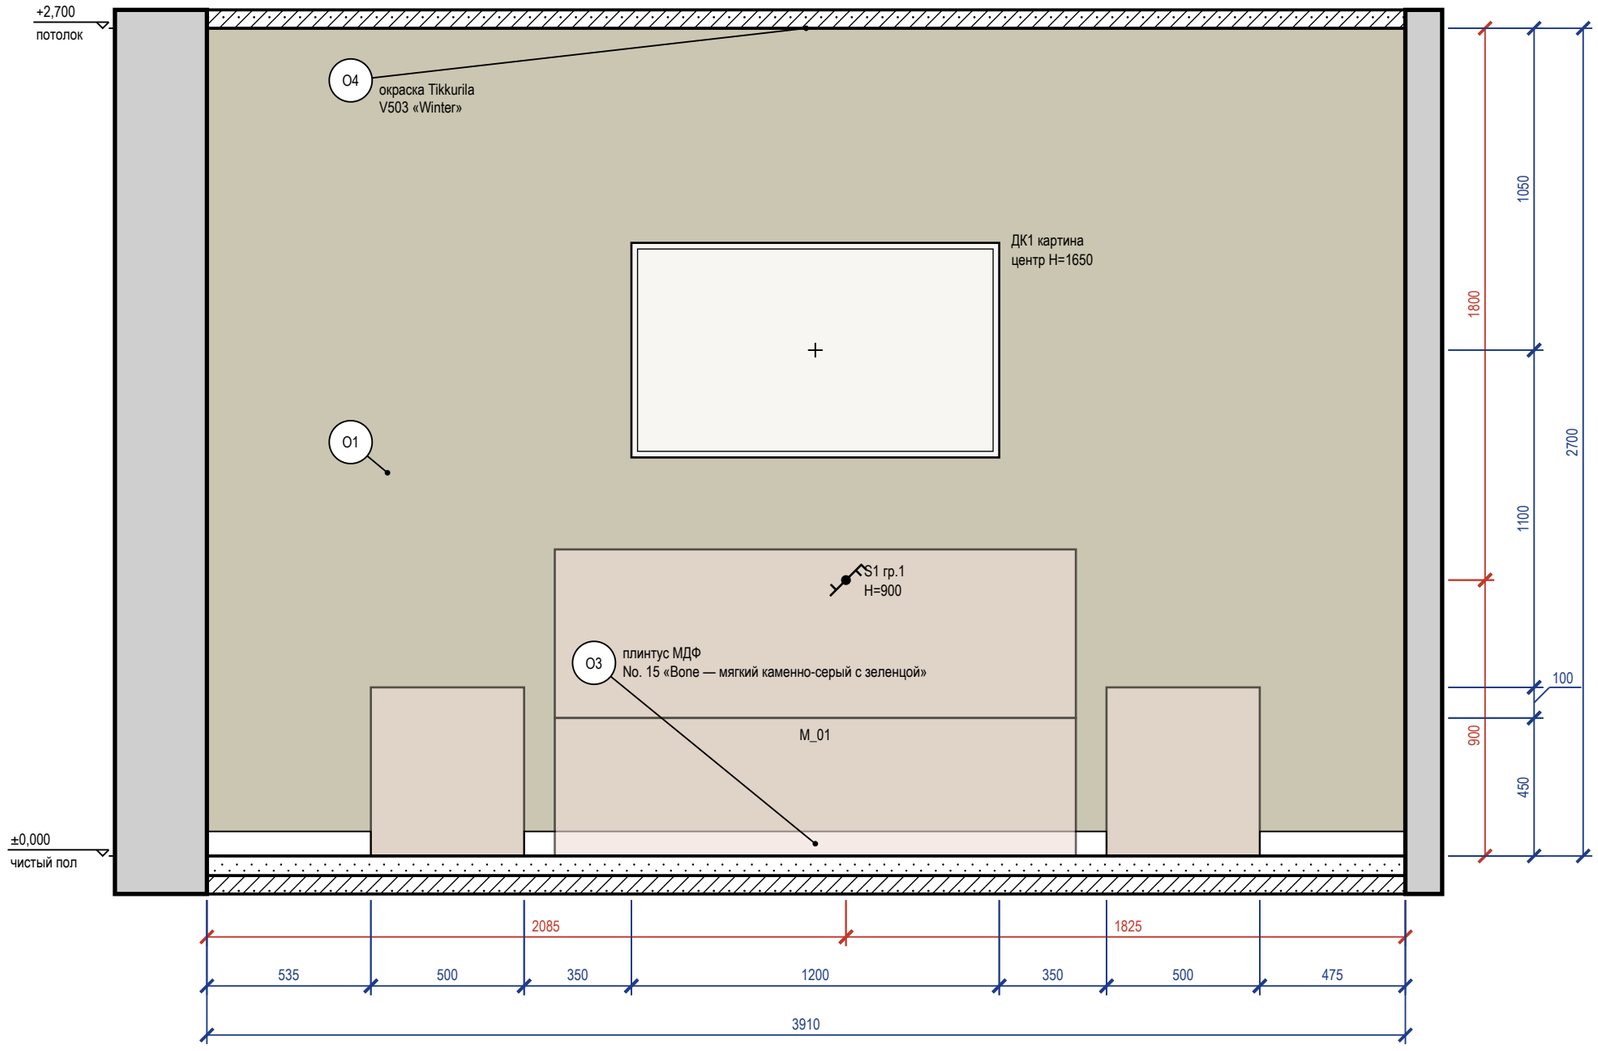


Схема развёрток (М 1:100)

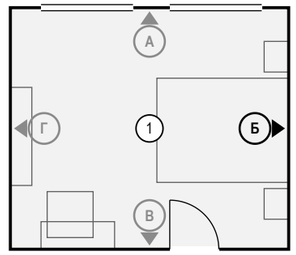

Ведомость отделки (на листе)

Марка	Поверхность	Материал, изделие	Цвет, код	Кол.
О1	стены	окраска, Farrow & Ball Modern Emulsion, матовая, подготовка Q3	Farrow & Ball No. 15 «Bone — мягкий каменно-серый с зеленцой»	10,6 м²
О3	плинтус	плинтус МДФ, h 80 мм, аналог: плинтус МДФ под покраску 80×16	Farrow & Ball No. 15 «Bone — мягкий каменно-серый с зеленцой»	2,9 м
О4	потолок	окраска, Tikkurila Anti-Reflex 2, глубокоматовая, подготовка Q3	Tikkurila V503 «Winter»	17,9 м²

Визуализация этой стены — лист 34



Примечания

1. Размеры — в мм от чистовых поверхностей стен; условные обозначения и общие указания — лист 2.
2. Картины и зеркала крепить к основанию по паспорту изделия (закладные и анкеры — в перечне скрытых работ); крест — ось центра предмета.

					Проект: Квартира с кабинетом
	Лист	№ док.	Подпись	Дата	
Дизайнер	Кырлан А.С.			21.10.26	Развёртка стены Б. Спальня (пом. 1)

Стадия	Лист	Листов
П	37	97

выпуск 18.10.2026 № 918b20bf25 · стр. 37 из 97

Правка к этому листу

Развёртка стены В


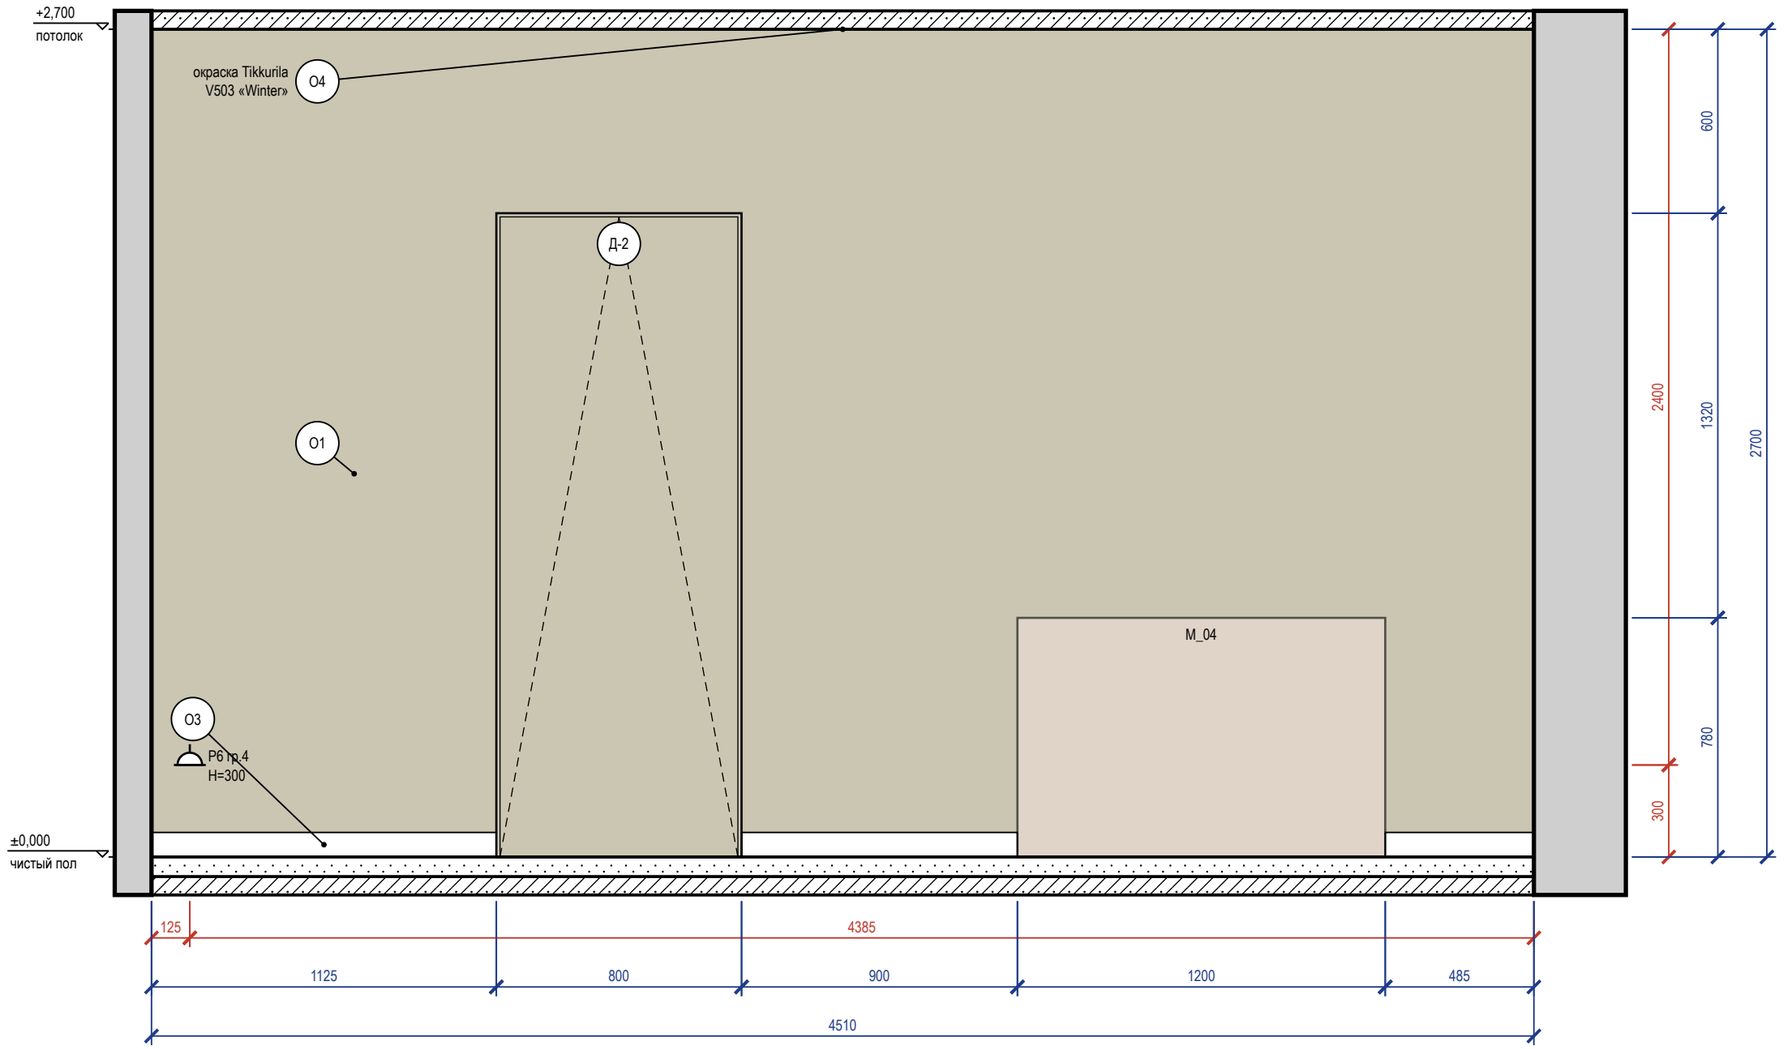


Схема развёрток (М 1:100)

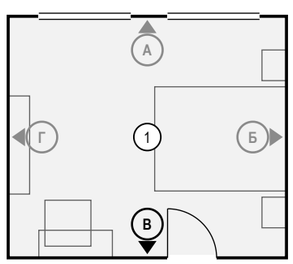

Ведомость отделки (на листе)

Марка	Поверхность	Материал, изделие	Цвет, код	Кол.
О1	стены	окраска, Farrow & Ball Modern Emulsion, матовая, подготовка Q3	Farrow & Ball No. 15 «Bone — мягкий каменно-серый с зеленцой»	10,5 м²
О3	плинтус	плинтус МДФ, h 80 мм, аналог: плинтус МДФ под покраску 80×16	Farrow & Ball No. 15 «Bone — мягкий каменно-серый с зеленцой»	2,5 м
О4	потолок	окраска, Tikkurila Anti-Reflex 2, глубокоматовая, подготовка Q3	Tikkurila V503 «Winter»	17,9 м²

Примечания

1. Размеры — в мм от чистовых поверхностей стен; условные обозначения и общие указания — лист 2.
2. Двери скрытого монтажа — полотно в плоскости стены, отделка стены по полотну, плинтус прерывается у короба (узел — на листе узлов).

					Проект: Квартира с кабинетом
	Лист	№ док.	Подпись	Дата	Развёртка стены В. Спальня (пом. 1)
Дизайнер	Кырлан А.С.			21.10.26	

Стадия	Лист	Листов
П	38	97

выпуск 18.10.2026 № 918b20bf25 · стр. 38 из 97

Правка к этому листу

Развёртка стены Г


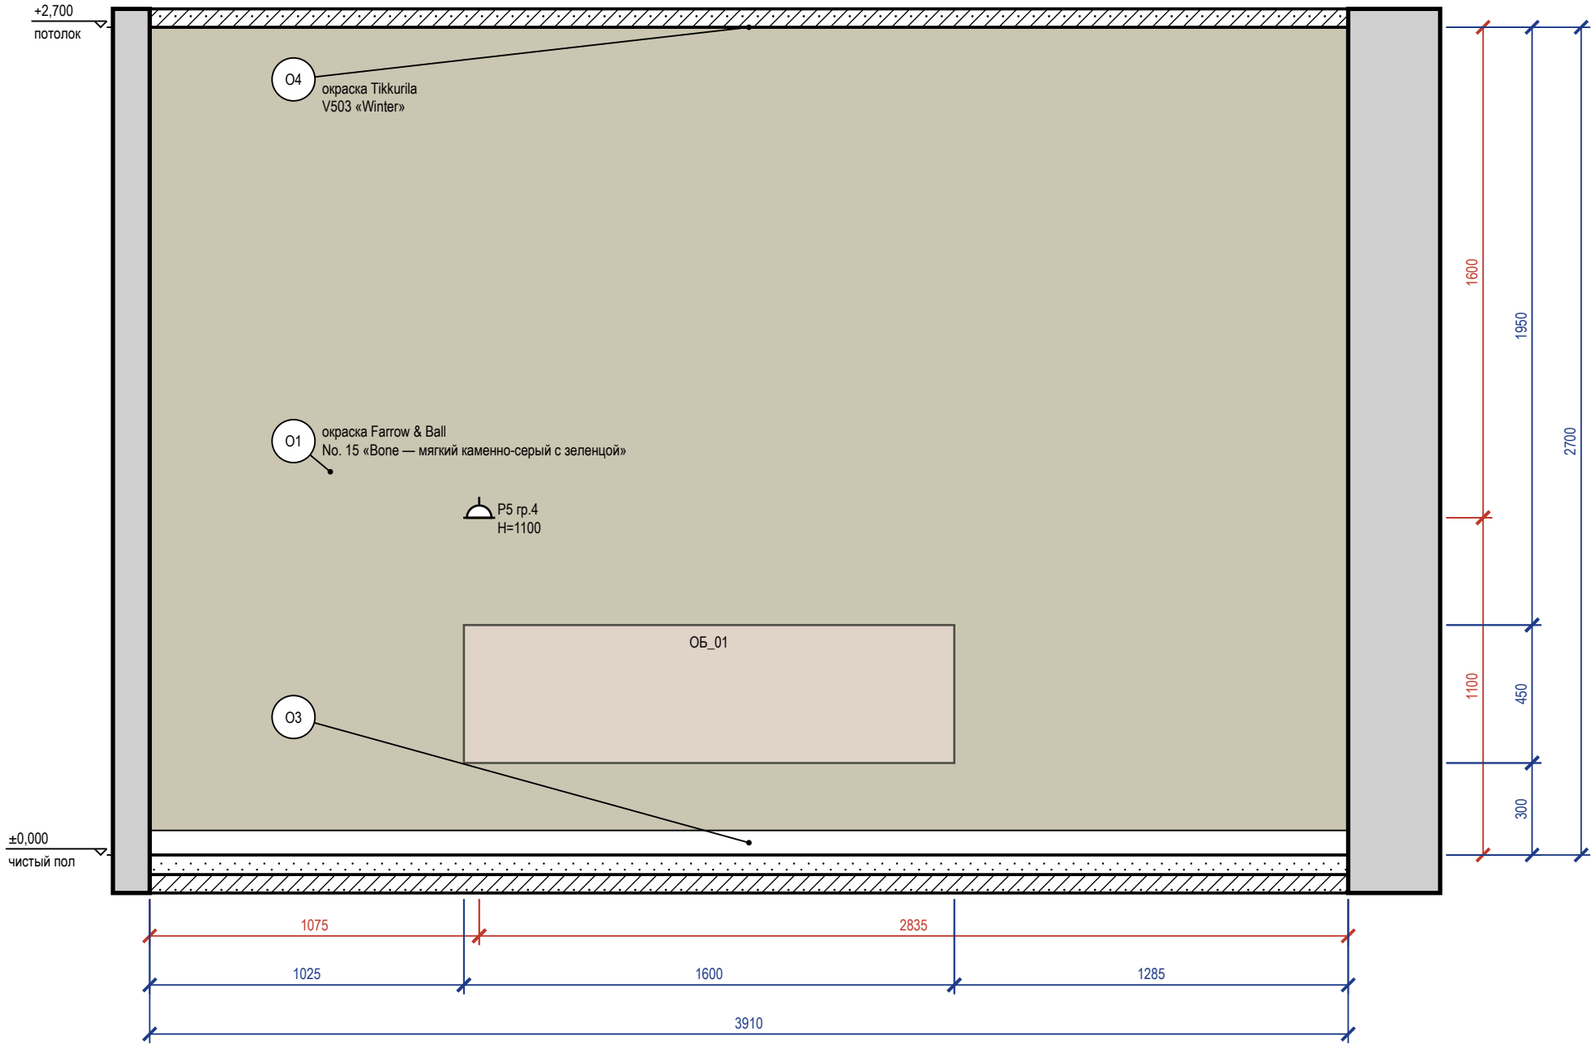


Схема развёрток (М 1:100)

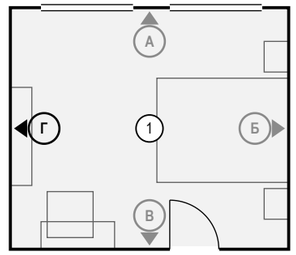

Ведомость отделки (на листе)

Марка	Поверхность	Материал, изделие	Цвет, код	Кол.
О1	стены	окраска, Farrow & Ball Modern Emulsion, матовая, подготовка Q3	Farrow & Ball No. 15 «Bone — мягкий каменно-серый с зеленцой»	10,6 м²
О3	плинтус	плинтус МДФ, h 80 мм, аналог: плинтус МДФ под покраску 80×16	Farrow & Ball No. 15 «Bone — мягкий каменно-серый с зеленцой»	3,9 м
О4	потолок	окраска, Tikkurila Anti-Reflex 2, глубокоматовая, подготовка Q3	Tikkurila V503 «Winter»	17,9 м²

Визуализация этой стены — лист 35



Примечания

1. Размеры — в мм от чистовых поверхностей стен; условные обозначения и общие указания — лист 2.

					Проект: Квартира с кабинетом
	Лист	№ док.	Подпись	Дата	
Дизайнер	Кырлан А.С.			21.10.26	Развёртка стены Г. Спальня (пом. 1)

Стадия	Лист	Листов
П	39	97

выпуск 18.10.2026 № 918b20bf25 · стр. 39 из 97

Правка к этому листу




					Проект: Квартира с кабинетом	
	Лист	№ док.	Подпись	Дата		
Дизайнер	Кырлан А.С.			21.10.26	Визуализация: Гардеробная-постирочная	Стадия / Лист / Листов
						П / 40 / 97

выпуск 18.10.2026 № 918b20bf25 · стр. 40 из 97

Правка к этому листу

Развёртка стены А

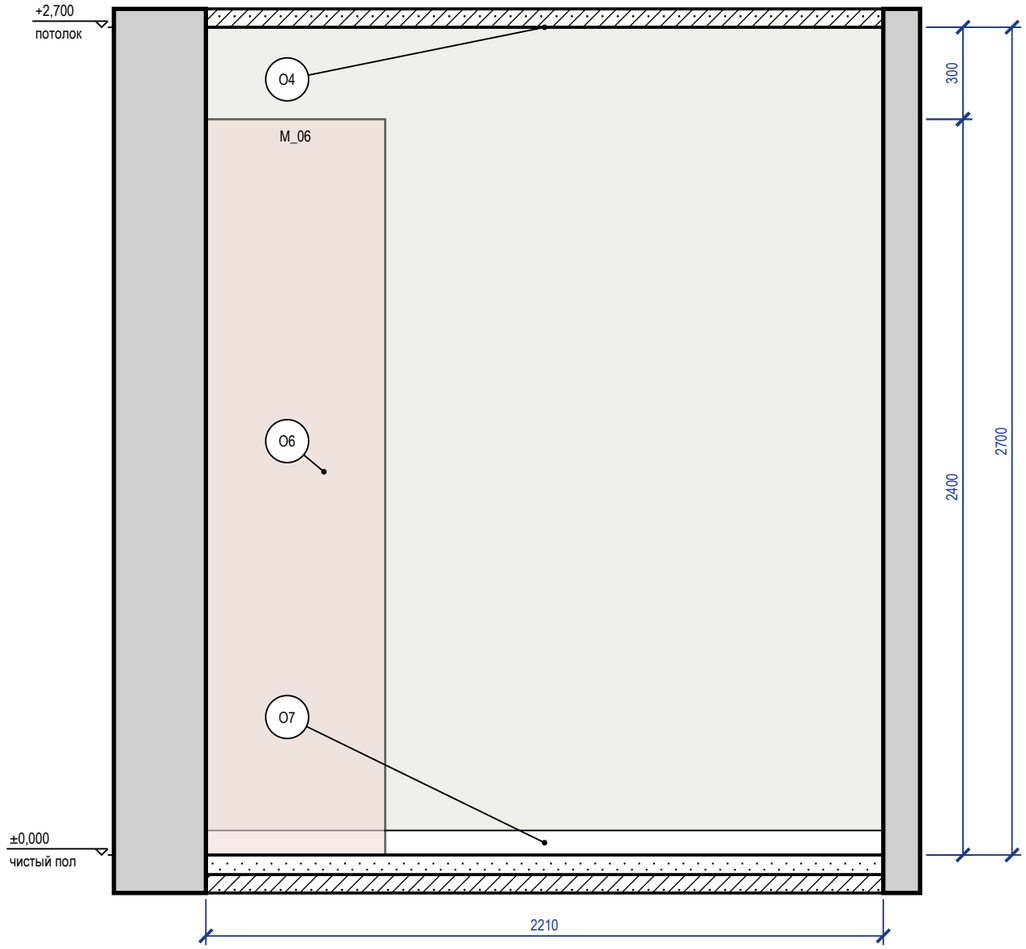

Развёртка стены Б


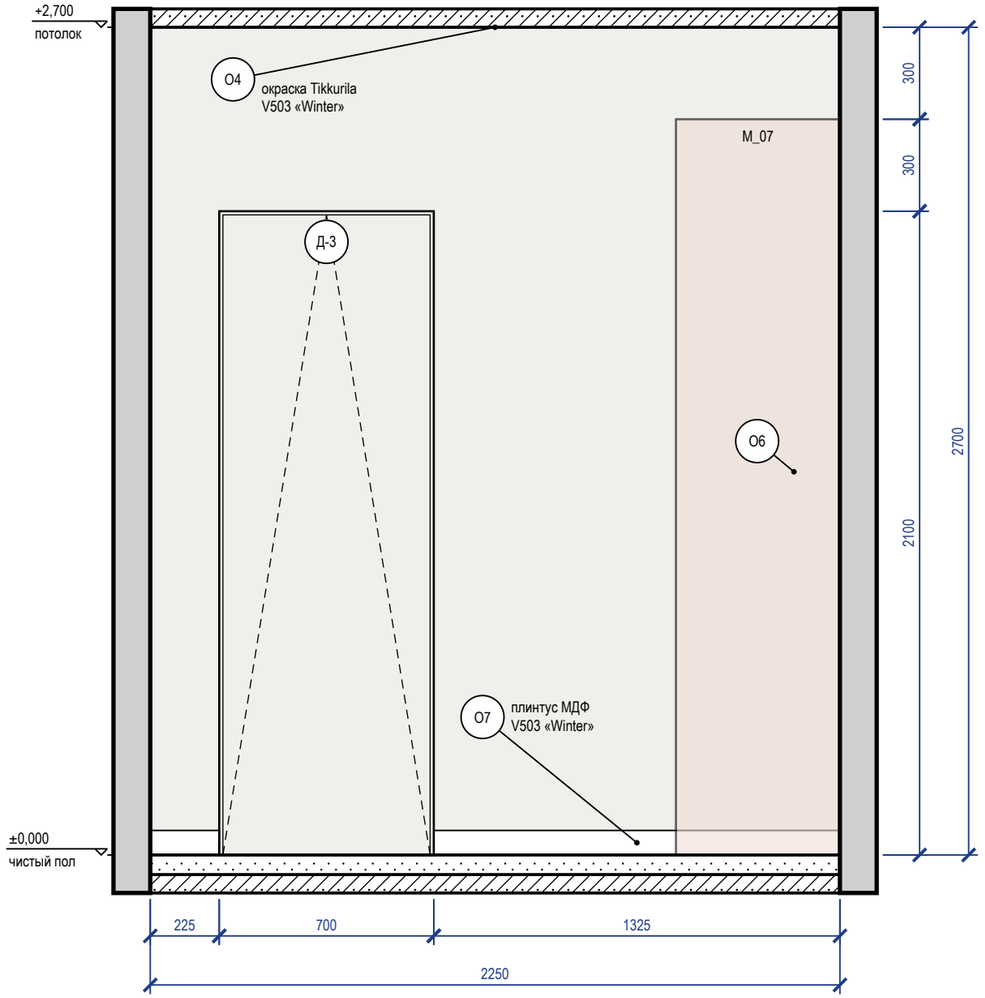


Схема развёрток (М 1:100)

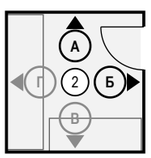

Ведомость отделки (на листе)

Марка	Поверхность	Материал, изделие	Цвет, код	Кол.
О4	потолок	окраска, Tikkurila Anti-Reflex 2, глубокоматовая, подготовка Q3	Tikkurila V503 «Winter»	5,1 м²
О6	стены	окраска, Tikkurila Harmony, матовая, подготовка Q3	Tikkurila V503 «Winter»	10,6 м²
О7	плинтус	плинтус МДФ, h 80 мм, аналог: плинтус МДФ под покраску 80×16	Tikkurila V503 «Winter»	3,8 м

Примечания

1. Размеры — в мм от чистовых поверхностей стен; условные обозначения и общие указания — лист 2.
2. Двери скрытого монтажа — полотно в плоскости стены, отделка стены по полотну, плинтус прерывается у короба (узел — на листе узлов).

	Лист	№ док.	Подпись	Дата
Дизайнер	Кырлан А.С.			21.10.26

Проект: Квартира с кабинетом


Развёртки стен А, Б.
Гардеробная-постирочная (пом. 2)

Стадия	Лист	Листов
П	41	97

выпуск 18.10.2026 № 918b20bf25 · стр. 41 из 97

Правка к этому листу

Развёртка стены В

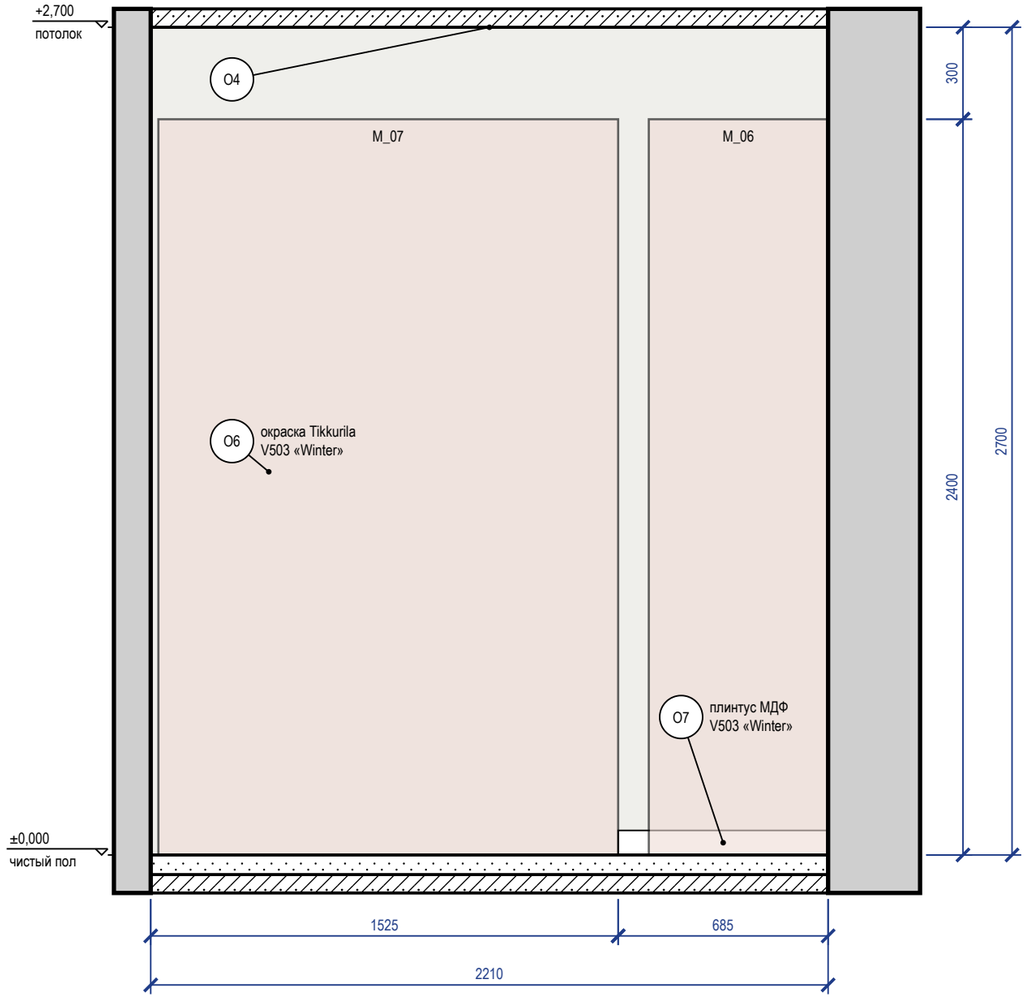

Развёртка стены Г


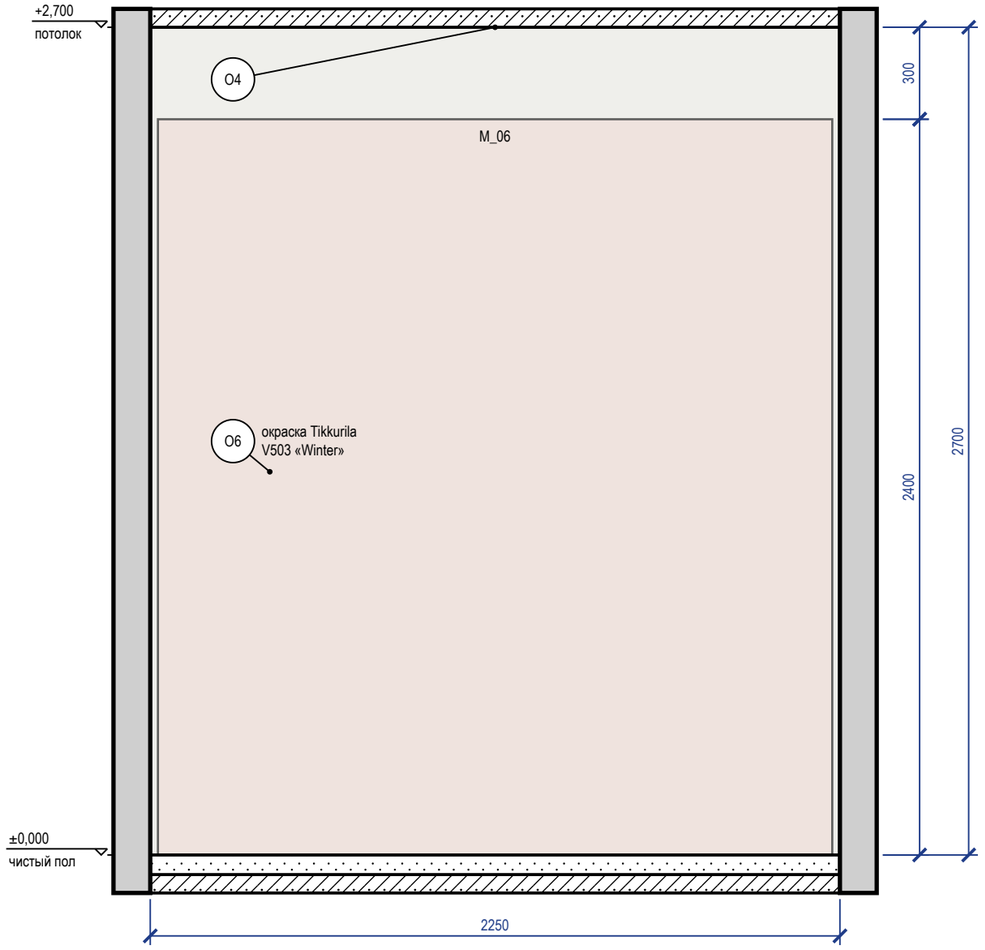


Схема развёрток (М 1:100)

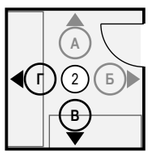

Ведомость отделки (на листе)

Марка	Поверхность	Материал, изделие	Цвет, код	Кол.
О4	потолок	окраска, Tikkurila Anti-Reflex 2, глубокоматовая, подготовка Q3	Tikkurila V503 «Winter»	5,1 м²
О6	стены	окраска, Tikkurila Harmony, матовая, подготовка Q3	Tikkurila V503 «Winter»	12 м²
О7	плинтус	плинтус МДФ, h 80 мм, аналог: плинтус МДФ под покраску 80×16	Tikkurila V503 «Winter»	0,7 м

Визуализация этой стены — лист 40



Примечания

1. Размеры — в мм от чистовых поверхностей стен; условные обозначения и общие указания — лист 2.

					Проект: Квартира с кабинетом
	Лист	№ док.	Подпись	Дата	Развёртки стен В, Г. Гардеробная-постирочная (пом. 2)
Дизайнер	Кырлан А.С.			21.10.26	

Стадия	Лист	Листов
П	42	97

выпуск 18.10.2026 № 918b20bf25 · стр. 42 из 97

Правка к этому листу



					Проект: Квартира с кабинетом	
	Лист	№ док.	Подпись	Дата		
Дизайнер	Кырлан А.С.			21.10.26	Визуализация кабинета	Стадия / Лист / Листов
						П / 43 / 97

выпуск 18.10.2026 № 918b20bf25 · стр. 43 из 97

Правка к этому листу



					Проект: Квартира с кабинетом
	Лист	№ док.	Подпись	Дата	Визуализация кабинета
Дизайнер	Кырлан А.С.			21.10.26	

Стадия	Лист	Листов
П	44	97

выпуск 18.10.2026 № 918b20bf25 · стр. 44 из 97

Правка к этому листу



					Проект: Квартира с кабинетом
	Лист	№ док.	Подпись	Дата	
Дизайнер	Кырлан А.С.			21.10.26	Визуализация кабинета

Стадия	Лист	Листов
П	45	97

выпуск 18.10.2026 № 918b20bf25 · стр. 45 из 97

Правка к этому листу

Развёртка стены А


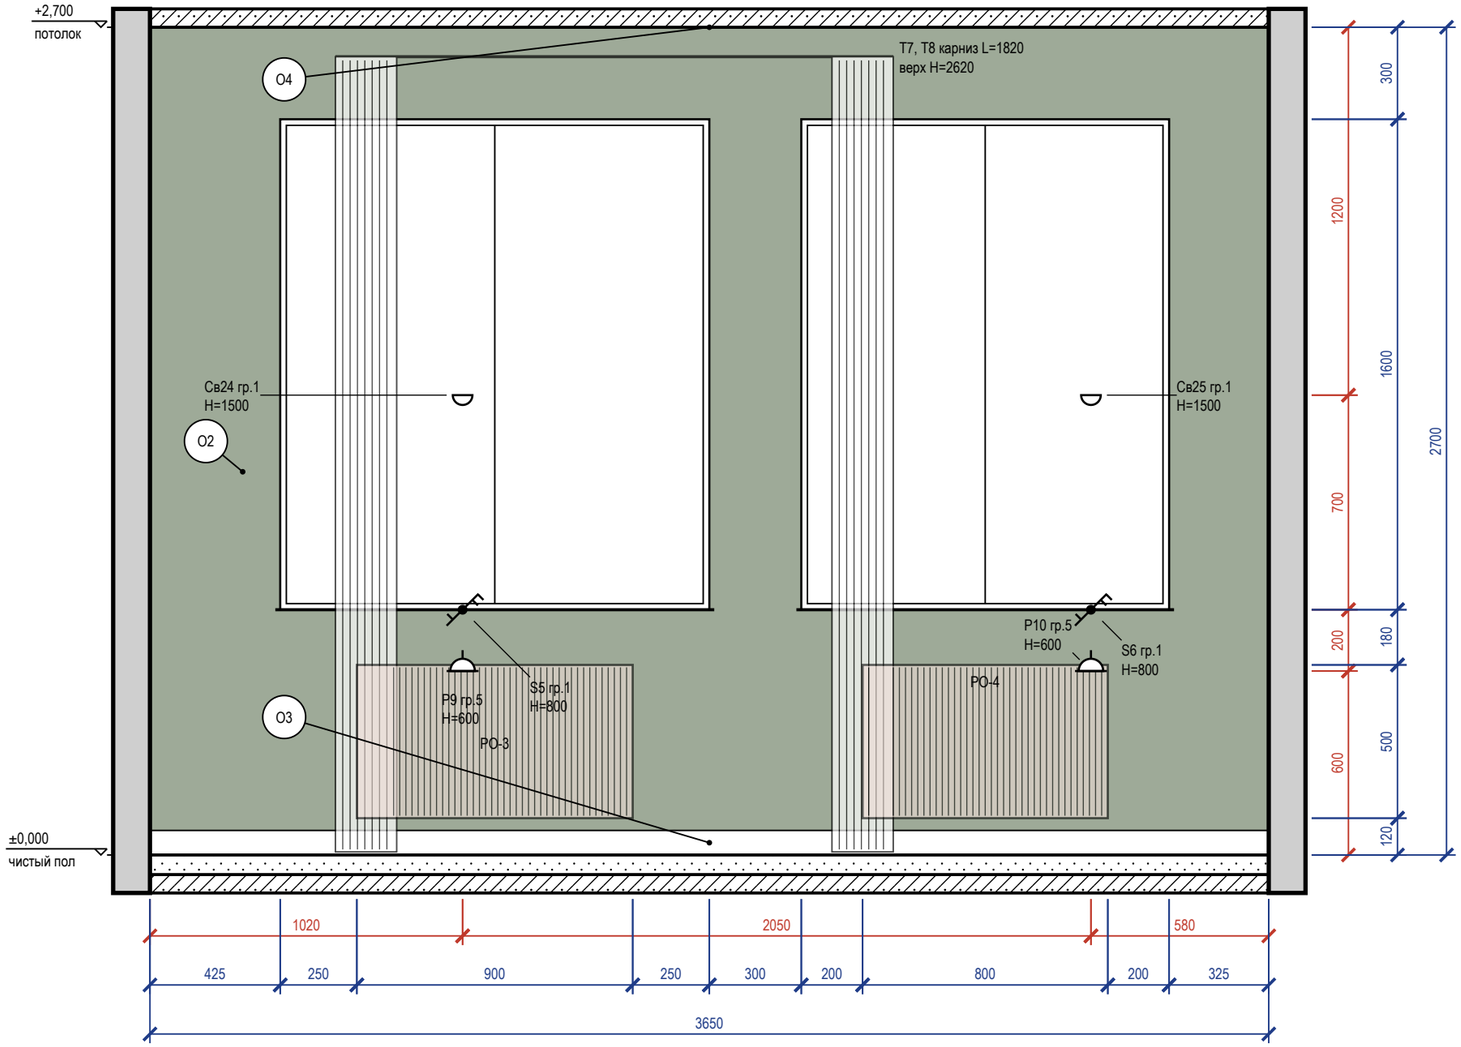


Схема развёрток (М 1:100)

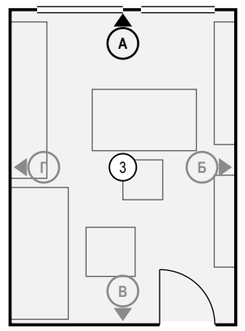

Ведомость отделки (на листе)

Марка	Поверхность	Материал, изделие	Цвет, код	Кол.
О2	акцентная стена	окраска, Farrow & Ball Modern Emulsion, матовая, подготовка Q3	Farrow & Ball No. 34 «Calke Green традиционный шалфей»	5,7 м²
О3	плинтус	плинтус МДФ, h 80 мм, аналог: плинтус МДФ под покраску 80×16	Farrow & Ball No. 15 «Bone — мягкий каменно-серый с зеленцой»	3,6 м
О4	потолок	окраска, Tikkurila Anti-Reflex 2, глубокоматовая, подготовка Q3	Tikkurila V503 «Winter»	18,9 м²

Визуализация этой стены — лист 43



Примечания

1. Размеры — в мм от чистовых поверхностей стен; условные обозначения и общие указания — лист 2.
2. Карнизы (шины) — по ведомости текстиля декоратора; длина L и верх H — по развёртке, крепление — до окраски потолка.
3. Линии узора (швы плитки, складки штор, рёбра радиаторов) прерываются у знаков и выносок — просвет между линиями не менее 0,7 мм.

					Проект: Квартира с кабинетом
	Лист	№ док.	Подпись	Дата	
Дизайнер	Кырлан А.С.			21.10.26	Развёртка стены А. Кабинет (пом. 3)

Стадия	Лист	Листов
П	46	97

выпуск 18.10.2026 № 918b20bf25 · стр. 46 из 97

Правка к этому листу

Развёртка стены Б


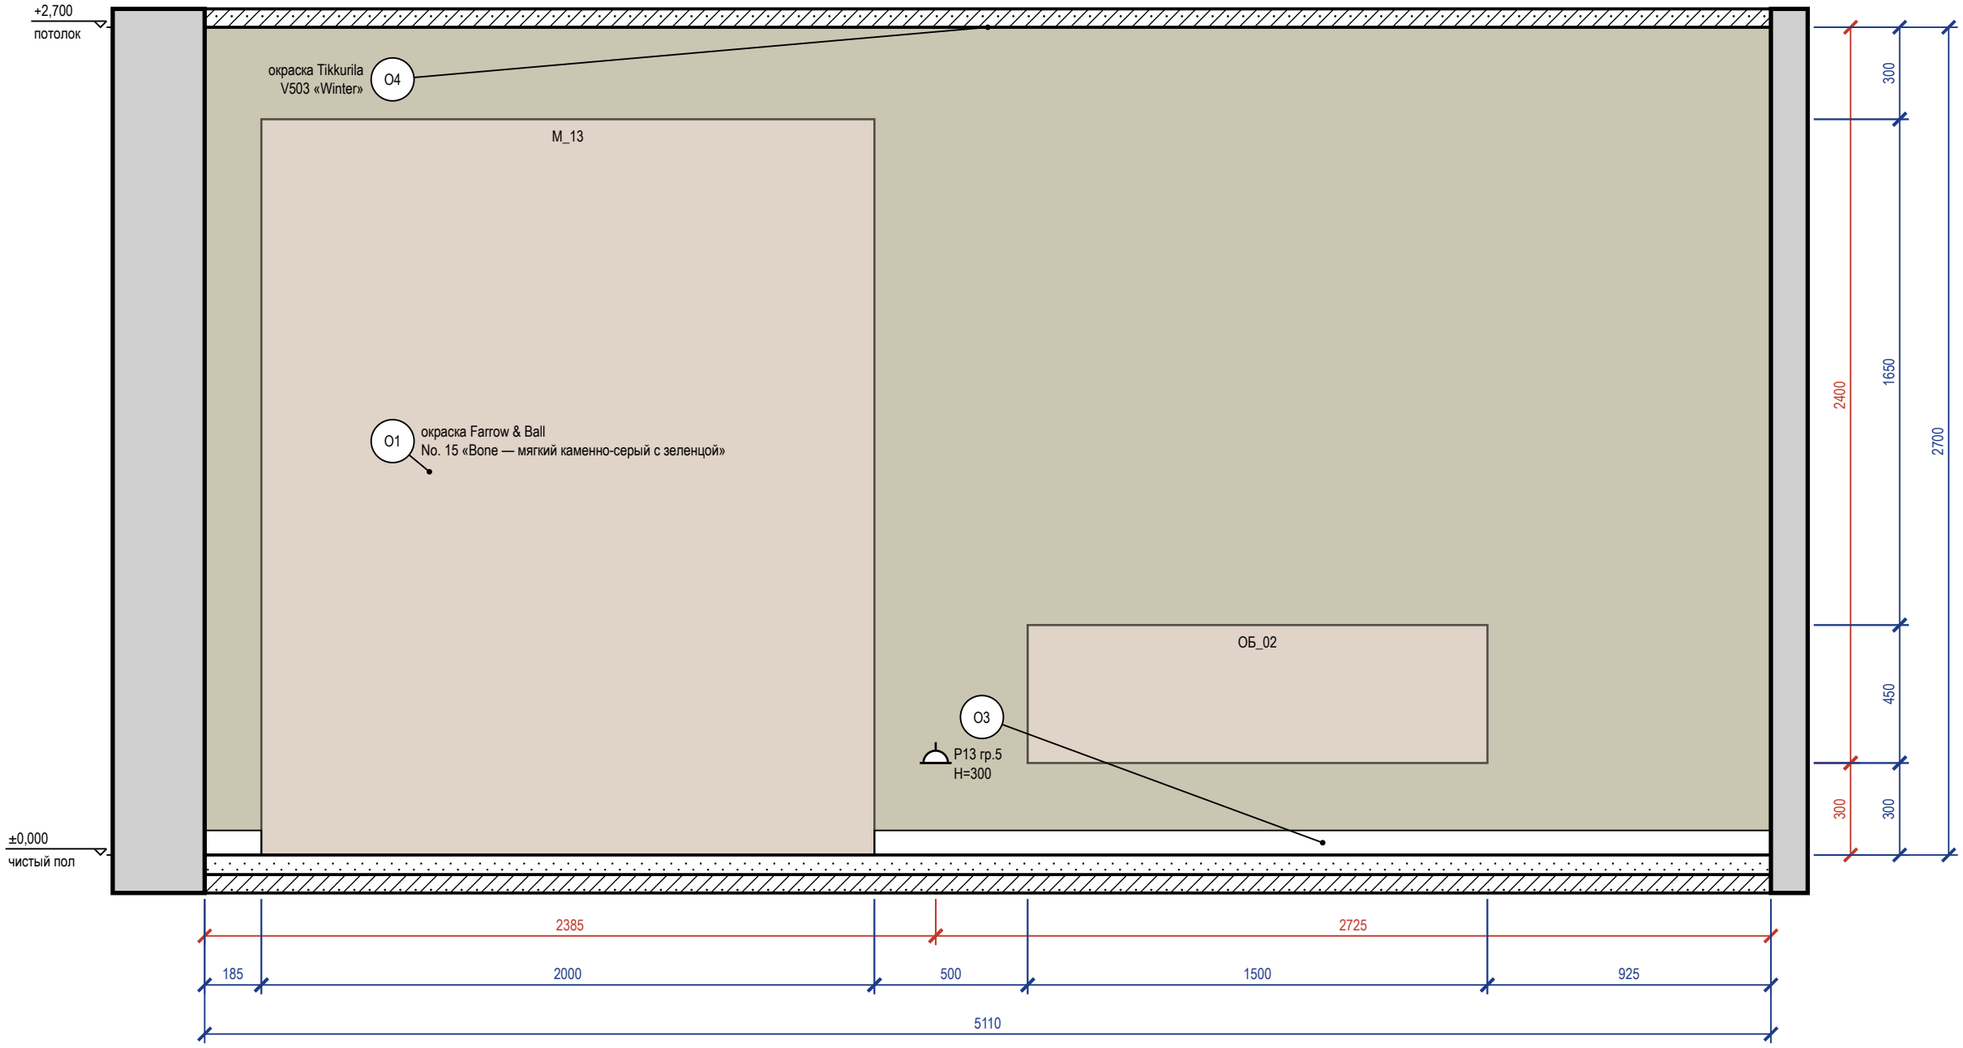


Схема развёрток (М 1:100)

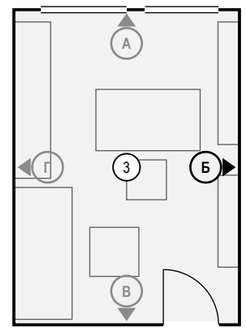

Ведомость отделки (на листе)

Марка	Поверхность	Материал, изделие	Цвет, код	Кол.
О1	стены	окраска, Farrow & Ball Modern Emulsion, матовая, подготовка Q3	Farrow & Ball No. 15 «Bone — мягкий каменно-серый с зеленцой»	13,8 м²
О3	плинтус	плинтус МДФ, h 80 мм, аналог: плинтус МДФ под покраску 80×16	Farrow & Ball No. 15 «Bone — мягкий каменно-серый с зеленцой»	3,1 м
О4	потолок	окраска, Tikkurila Anti-Reflex 2, глубокоматовая, подготовка Q3	Tikkurila V503 «Winter»	18,9 м²

Визуализация этой стены — лист 44



Примечания

1. Размеры — в мм от чистовых поверхностей стен; условные обозначения и общие указания — лист 2.

					Проект: Квартира с кабинетом
	Лист	№ док.	Подпись	Дата	Развёртка стены Б. Кабинет (пом. 3)
Дизайнер	Кырлан А.С.			21.10.26	

Стадия	Лист	Листов
П	47	97

выпуск 18.10.2026 № 918b20bf25 · стр. 47 из 97

Правка к этому листу

Развёртка стены В


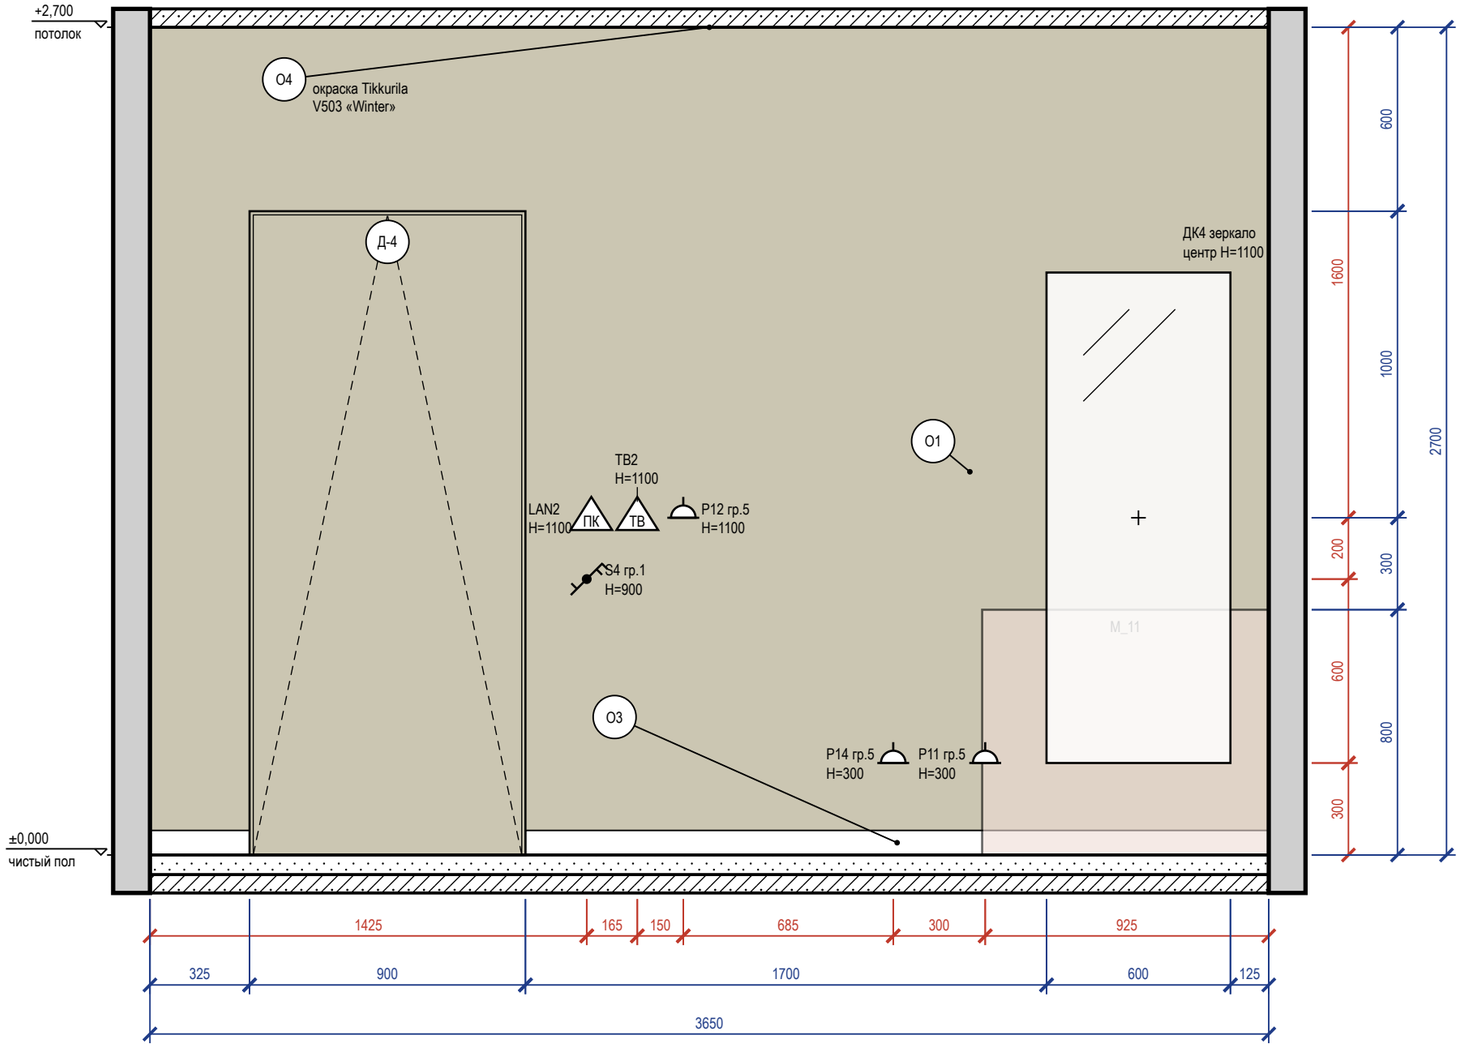


Схема развёрток (М 1:100)

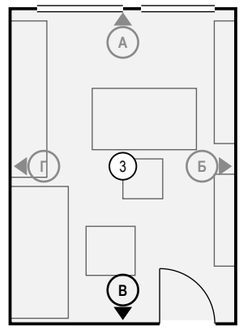

Ведомость отделки (на листе)

Марка	Поверхность	Материал, изделие	Цвет, код	Кол.
О1	стены	окраска, Farrow & Ball Modern Emulsion, матовая, подготовка Q3	Farrow & Ball No. 15 «Bone — мягкий каменно-серый с зеленцой»	8 м²
О3	плинтус	плинтус МДФ, h 80 мм, аналог: плинтус МДФ под покраску 80×16	Farrow & Ball No. 15 «Bone — мягкий каменно-серый с зеленцой»	2,8 м
О4	потолок	окраска, Tikkurila Anti-Reflex 2, глубокоматовая, подготовка Q3	Tikkurila V503 «Winter»	18,9 м²

Примечания

1. Размеры — в мм от чистовых поверхностей стен; условные обозначения и общие указания — лист 2.
2. Картины и зеркала крепить к основанию по паспорту изделия (закладные и анкеры — в перечне скрытых работ); крест — ось центра предмета.
3. Двери скрытого монтажа — полотно в плоскости стены, отделка стены по полотну, плинтус прерывается у короба (узел — на листе узлов).

					Проект: Квартира с кабинетом
	Лист	№ док.	Подпись	Дата	Развёртка стены В. Кабинет (пом. 3)
Дизайнер	Кырлан А.С.			21.10.26	

Стадия	Лист	Листов
П	48	97

выпуск 18.10.2026 № 918b20bf25 · стр. 48 из 97

Правка к этому листу

Развёртка стены Г


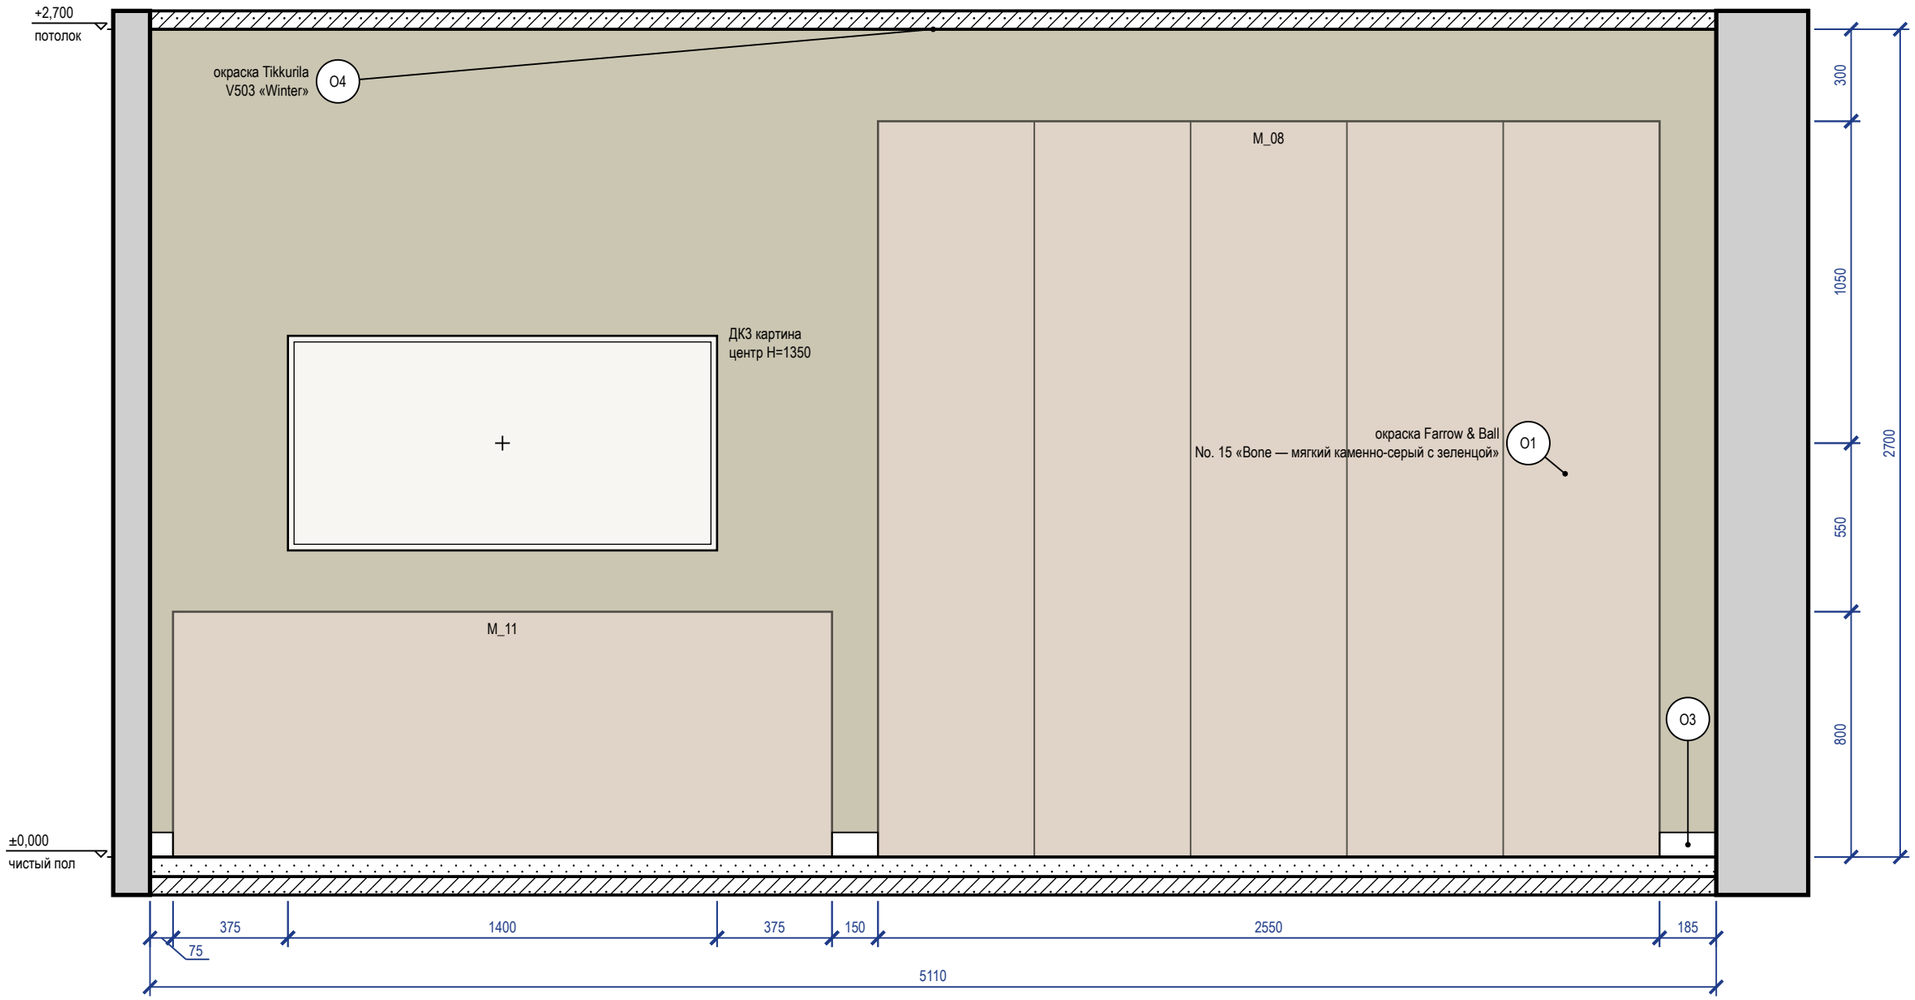



Схема развёрток (М 1:100)

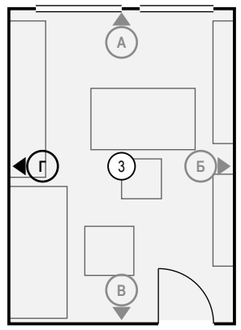

Ведомость отделки (на листе)

Марка	Поверхность	Материал, изделие	Цвет, код	Кол.
O1	стены	окраска, Farrow & Ball Modern Emulsion, матовая, подготовка Q3	Farrow & Ball No. 15 «Bone — мягкий каменно-серый с зеленцой»	13,8 м²
O3	плинтус	плинтус МДФ, h 80 мм, аналог: плинтус МДФ под покраску 80×16	Farrow & Ball No. 15 «Bone — мягкий каменно-серый с зеленцой»	0,4 м
O4	потолок	окраска, Tikkurila Anti-Reflex 2, глубокоматовая, подготовка Q3	Tikkurila V503 «Winter»	18,9 м²

Визуализация этой стены — лист 45

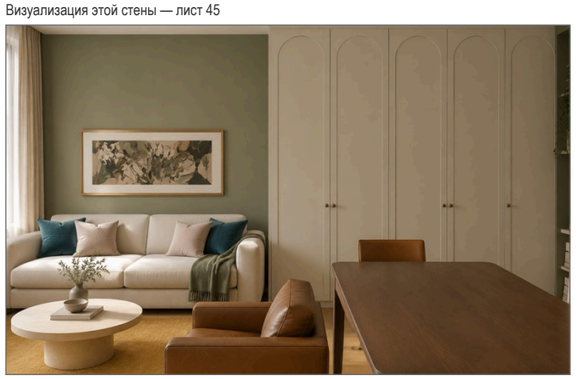

Примечания

1. Размеры — в мм от чистовых поверхностей стен; условные обозначения и общие указания — лист 2.
2. Картины и зеркала крепить к основанию по паспорту изделия (закладные и анкеры — в перечне скрытых работ); крест — ось центра предмета.

					Проект: Квартира с кабинетом
	Лист	№ док.	Подпись	Дата	
Дизайнер	Кырлан А.С.			21.10.26	Развёртка стены Г. Кабинет (пом. 3)

Стадия	Лист	Листов
П	49	97

выпуск 18.10.2026 № 918b20bf25 · стр. 49 из 97

Правка к этому листу



					Проект: Квартира с кабинетом
	Лист	№ док.	Подпись	Дата	
Дизайнер	Кырлан А.С.			21.10.26	Визуализация кухни-гостиной

Стадия	Лист	Листов
П	50	97

выпуск 18.10.2026 № 918b20bf25 · стр. 50 из 97

Правка к этому листу



					Проект: Квартира с кабинетом	
	Лист	№ док.	Подпись	Дата		
Дизайнер	Кырлан А.С.			21.10.26	Визуализация кухни-гостиной	Стадия / Лист / Листов
						П / 51 / 97

выпуск 18.10.2026 № 918b20bf25 · стр. 51 из 97

Правка к этому листу



					Проект: Квартира с кабинетом	
	Лист	№ док.	Подпись	Дата		
Дизайнер	Кырлан А.С.			21.10.26	Визуализация кухни-гостиной	Стадия: П; Лист: 52; Листов: 97

выпуск 18.10.2026 № 918b20bf25 · стр. 52 из 97

Правка к этому листу



					Проект: Квартира с кабинетом	
	Лист	№ док.	Подпись	Дата		
Дизайнер	Кырлан А.С.			21.10.26	Визуализация кухни-гостиной	Стадия / Лист / Листов
						П / 53 / 97

выпуск 18.10.2026 № 918b20bf25 · стр. 53 из 97

Правка к этому листу

Развёртка стены Г


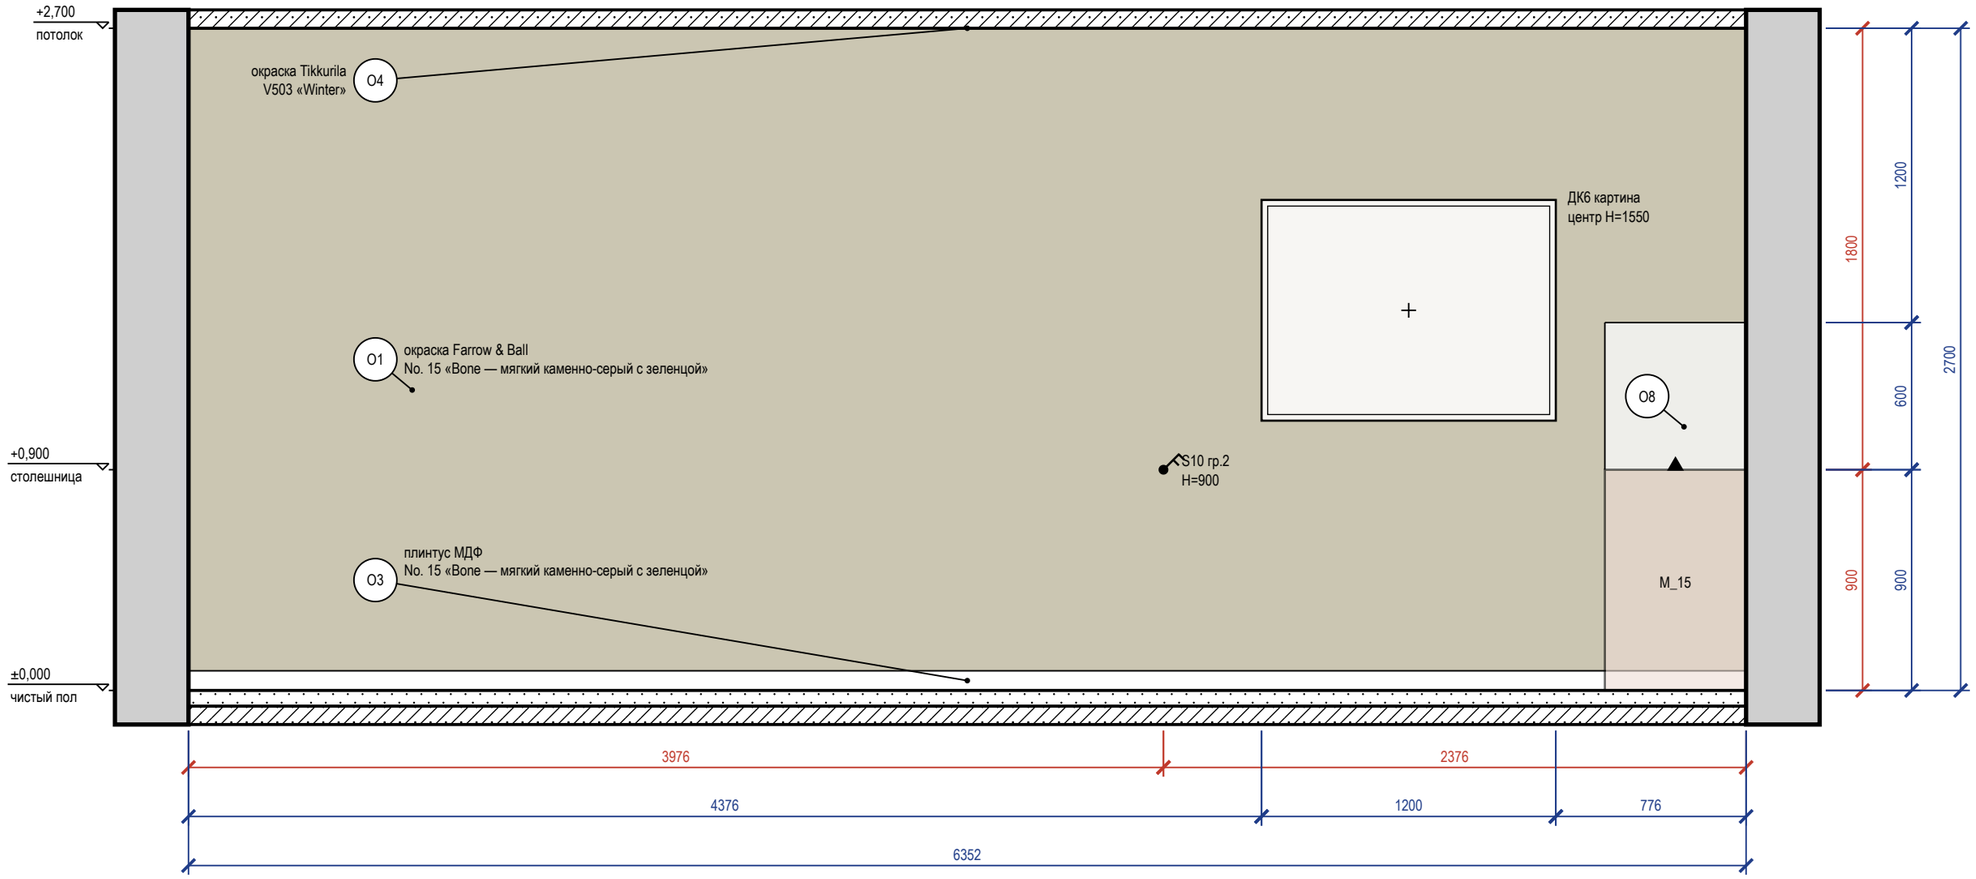


Схема развёрток (М 1:100)

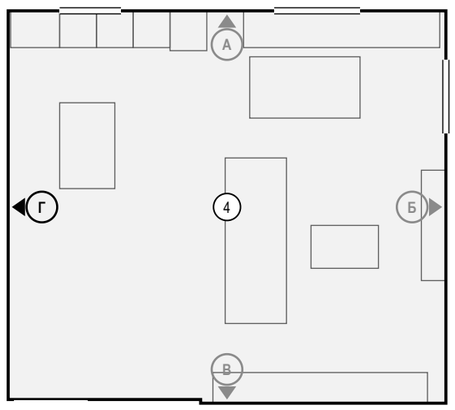

Ведомость отделки (на листе)

Марка	Поверхность	Материал, изделие	Цвет, код	Кол.
О1	стены	окраска, Farrow & Ball Modern Emulsion, матовая, подготовка Q3	Farrow & Ball No. 15 «Bone — мягкий каменно-серый с зеленцой»	16,8 м²
О3	плинтус	плинтус МДФ, h 80 мм, аналог: плинтус МДФ под покраску 80×16	Farrow & Ball No. 15 «Bone — мягкий каменно-серый с зеленцой»	6,4 м
О4	потолок	окраска, Tikkurila Anti-Reflex 2, глубокоматовая, подготовка Q3	Tikkurila V503 «Winter»	45,5 м²
О8	фартук	керамогранит, 1200×600×9 мм, аналог: керамогранит под травертин, матовый, затирка CG2WA		0,3 м²

Визуализация этой стены — лист 53



Примечания

1. Размеры — в мм от чистовых поверхностей стен; условные обозначения и общие указания — лист 2.
2. Картины и зеркала крепить к основанию по паспорту изделия (закладные и анкеры — в перечне скрытых работ); крест — ось центра предмета.
3. Высота фартука принята 600 мм над столешницей там, где нет навесных модулей и высота фартука не задана.
4. Выводы кухонной техники — по утверждённому проекту кухни: привязки выводов даются от осей модулей гарнитура.

	Лист	№ док.	Подпись	Дата
Дизайнер	Кырлан А.С.			21.10.26

Проект: Квартира с кабинетом

Развёртка стены Г. Кухня-гостиная (пом. 4), кухонный фронт

Стадия	Лист	Листов
П	54	97

выпуск 18.10.2026 № 918b20bf25 · стр. 54 из 97

Правка к этому листу

Развёртка стены А


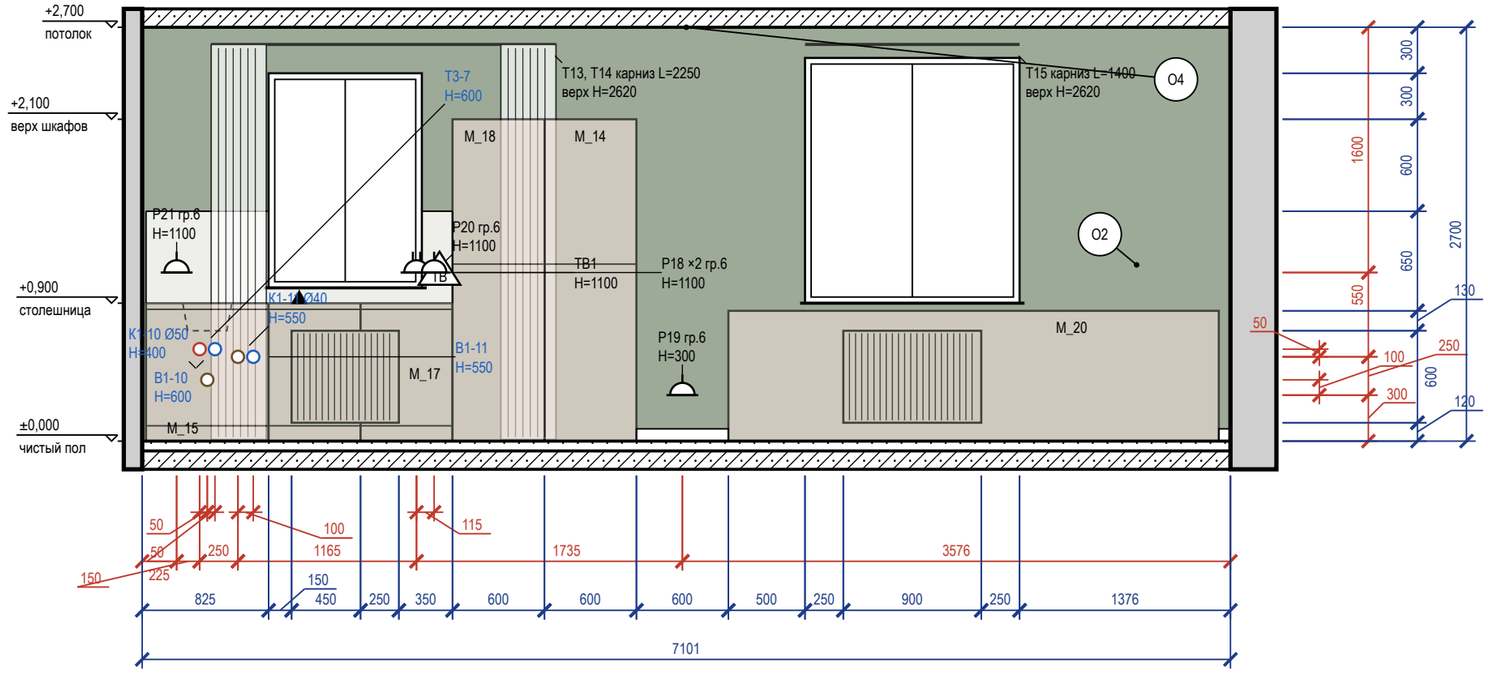


Схема развёрток (М 1:100)

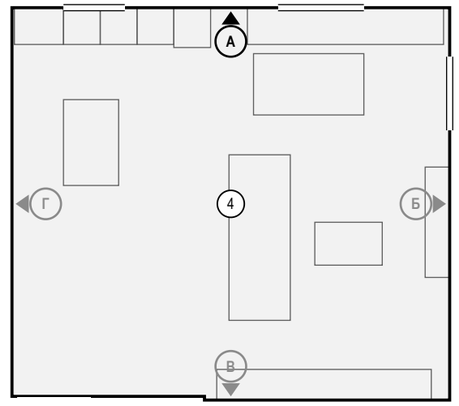

Ведомость отделки (на листе)

Марка	Поверхность	Материал, изделие	Цвет, код	Кол.
О2	акцентная стена	окраска, Farrow & Ball Modern Emulsion, матовая, подготовка Q3	Farrow & Ball No. 34 «Calke Green традиционный шалфей»	14,3 м²
О3	плинтус	плинтус МДФ, h 80 мм, аналог: плинтус МДФ под покраску 80×16	Farrow & Ball No. 15 «Bone — мягкий каменно-серый с зеленцой»	0,7 м
О4	потолок	окраска, Tikkurila Anti-Reflex 2, глубокоматовая, подготовка Q3	Tikkurila V503 «Winter»	45,5 м²
О8	фартук	керамогранит, 1200×600×9 мм, аналог: керамогранит под травертин, матовый, затирка CG2WA		0,7 м²

Визуализация этой стены — лист 50



Примечания

1. Размеры — в мм от чистовых поверхностей стен; условные обозначения и общие указания — лист 2.
2. Выводы ВК — коды и высоты по листу выводов сантехники.
3. Карнизы (шины) — по ведомости текстиля декоратора; длина L и верх H — по развёртке, крепление — до окраски потолка.
4. Высота фартука принята 600 мм над столешницей там, где нет навесных модулей и высота фартука не задана.
5. Выводы кухонной техники — по утверждённому проекту кухни: привязки выводов даются от осей модулей гарнитура.

					Проект: Квартира с кабинетом
	Лист	№ док.	Подпись	Дата	Развёртка стены А. Кухня-гостиная (пом. 4), кухонный фронт
Дизайнер	Кырлан А.С.			21.10.26	

Стадия	Лист	Листов
П	55	97

выпуск 18.10.2026 № 918b20bf25 · стр. 55 из 97

Правка к этому листу

Развёртка стены Б


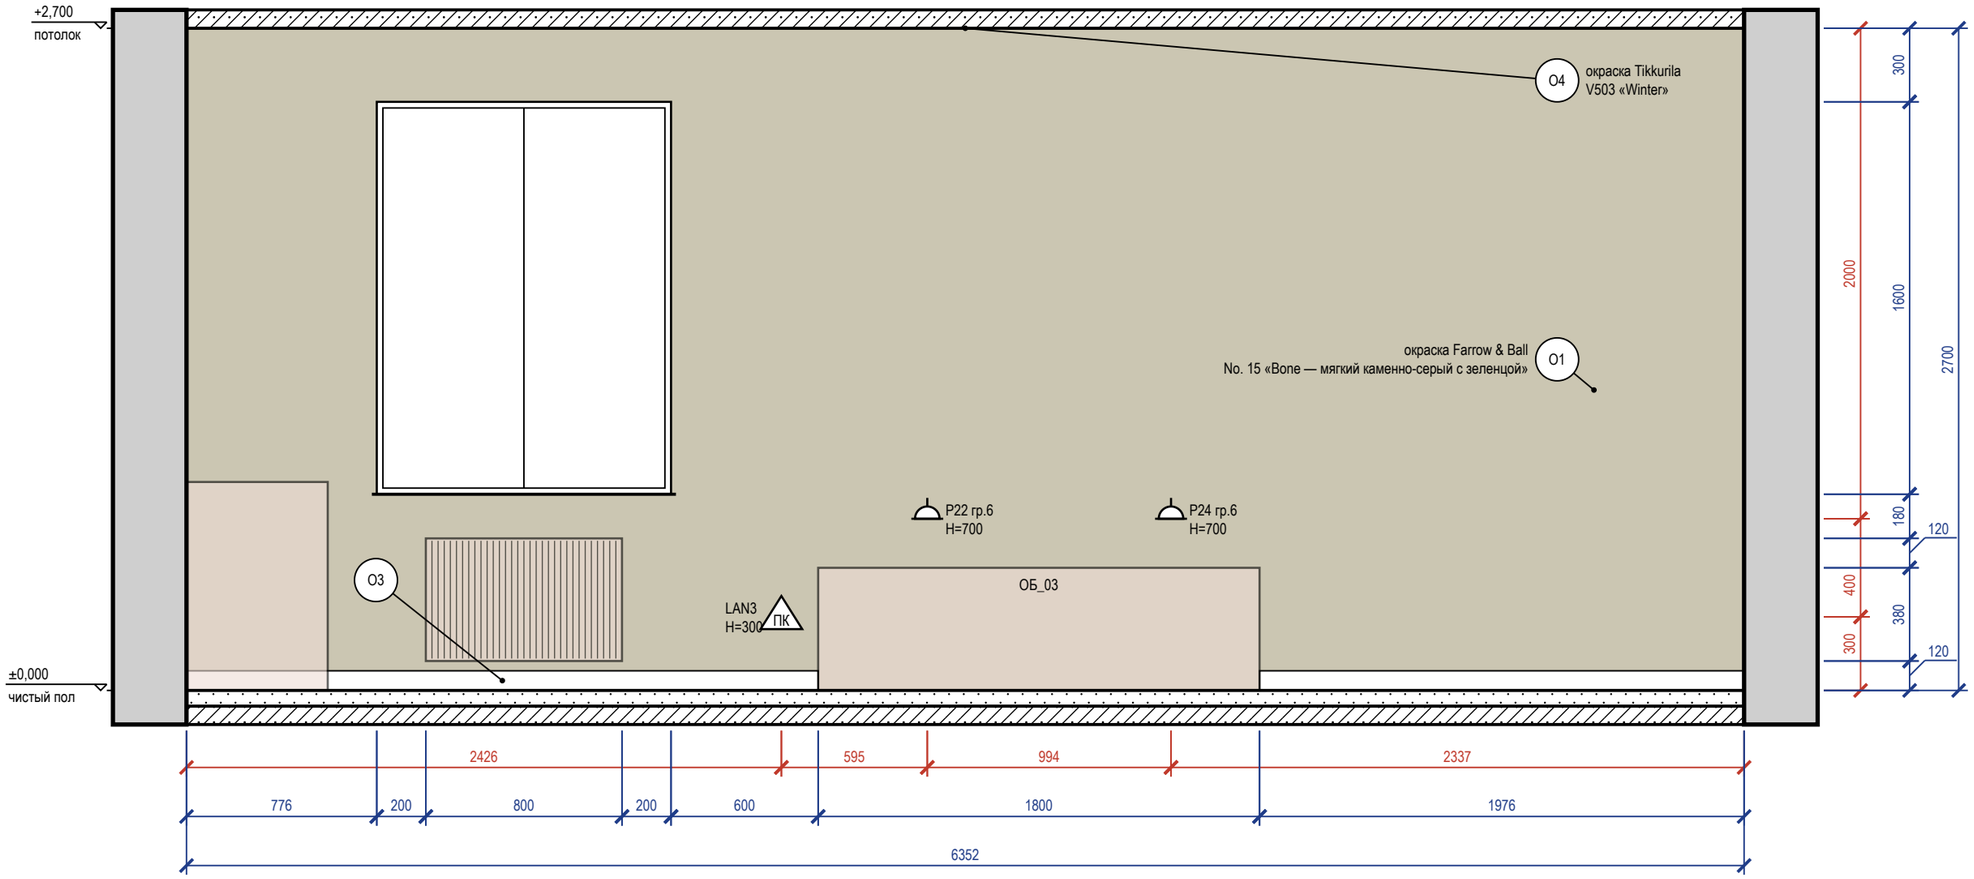


Схема развёрток (М 1:100)

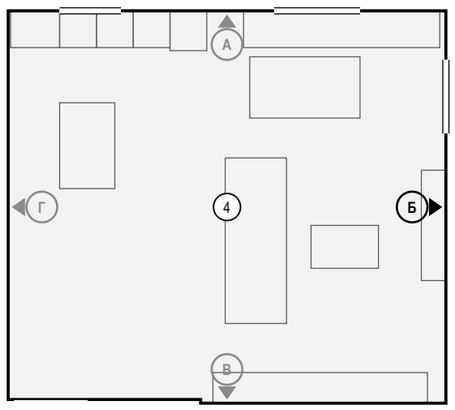

Ведомость отделки (на листе)

Марка	Поверхность	Материал, изделие	Цвет, код	Кол.
О1	стены	окраска, Farrow & Ball Modern Emulsion, матовая, подготовка Q3	Farrow & Ball No. 15 «Bone — мягкий каменно-серый с зеленцой»	15,2 м²
О3	плинтус	плинтус МДФ, h 80 мм, аналог: плинтус МДФ под покраску 80×16	Farrow & Ball No. 15 «Bone — мягкий каменно-серый с зеленцой»	4,6 м
О4	потолок	окраска, Tikkurila Anti-Reflex 2, глубокоматовая, подготовка Q3	Tikkurila V503 «Winter»	45,5 м²

Визуализация этой стены — лист 51



Примечания

1. Размеры — в мм от чистовых поверхностей стен; условные обозначения и общие указания — лист 2.

	Лист	№ док.	Подпись	Дата	Проект: Квартира с кабинетом
Дизайнер	Кырлан А.С.			21.10.26	Развёртка стены Б. Кухня-гостиная (пом. 4)

Стадия	Лист	Листов
П	56	97

выпуск 18.10.2026 № 918b20bf25 · стр. 56 из 97

Правка к этому листу

Развёртка стены В


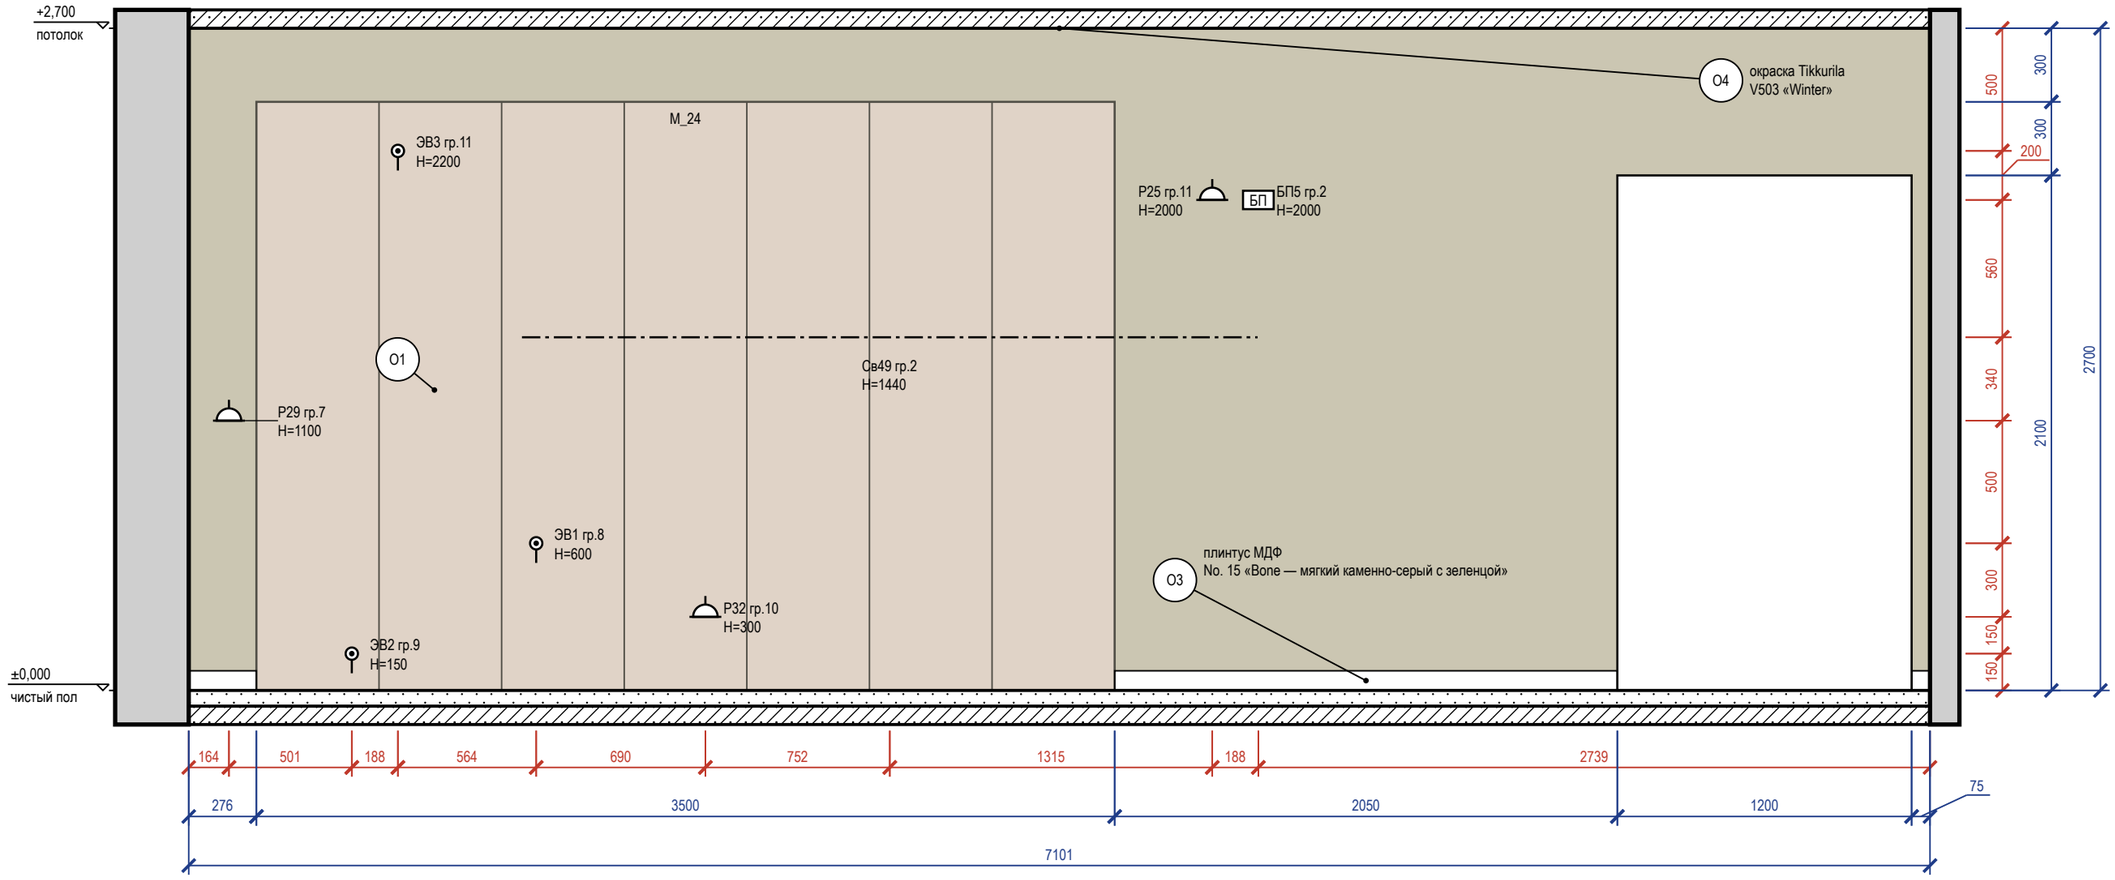


Схема развёрток (М 1:100)

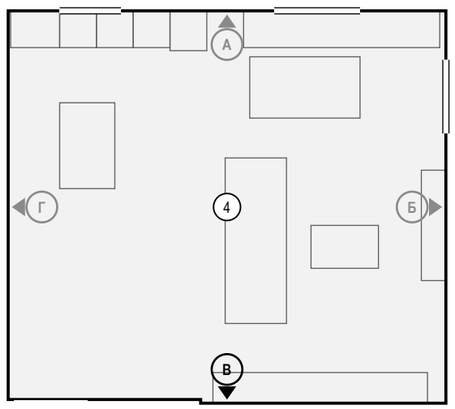

Ведомость отделки (на листе)

Марка	Поверхность	Материал, изделие	Цвет, код	Кол.
О1	стены	окраска, Farrow & Ball Modern Emulsion, матовая, подготовка Q3	Farrow & Ball No. 15 «Bone — мягкий каменно-серый с зеленцой»	16,7 м²
О3	плинтус	плинтус МДФ, h 80 мм, аналог: плинтус МДФ под покраску 80×16	Farrow & Ball No. 15 «Bone — мягкий каменно-серый с зеленцой»	2,4 м
О4	потолок	окраска, Tikkurila Anti-Reflex 2, глубокоматовая, подготовка Q3	Tikkurila V503 «Winter»	45,5 м²

Визуализация этой стены — лист 52



Примечания


1. Размеры — в мм от чистовых поверхностей стен; условные обозначения и общие указания — лист 2.

	Лист	№ док.	Подпись	Дата	Проект: Квартира с кабинетом
Дизайнер	Кырлан А.С.			21.10.26	Развёртка стены В. Кухня-гостиная (пом. 4)

Стадия	Лист	Листов
П	57	97

выпуск 18.10.2026 № 918b20bf25 · стр. 57 из 97

Правка к этому листу

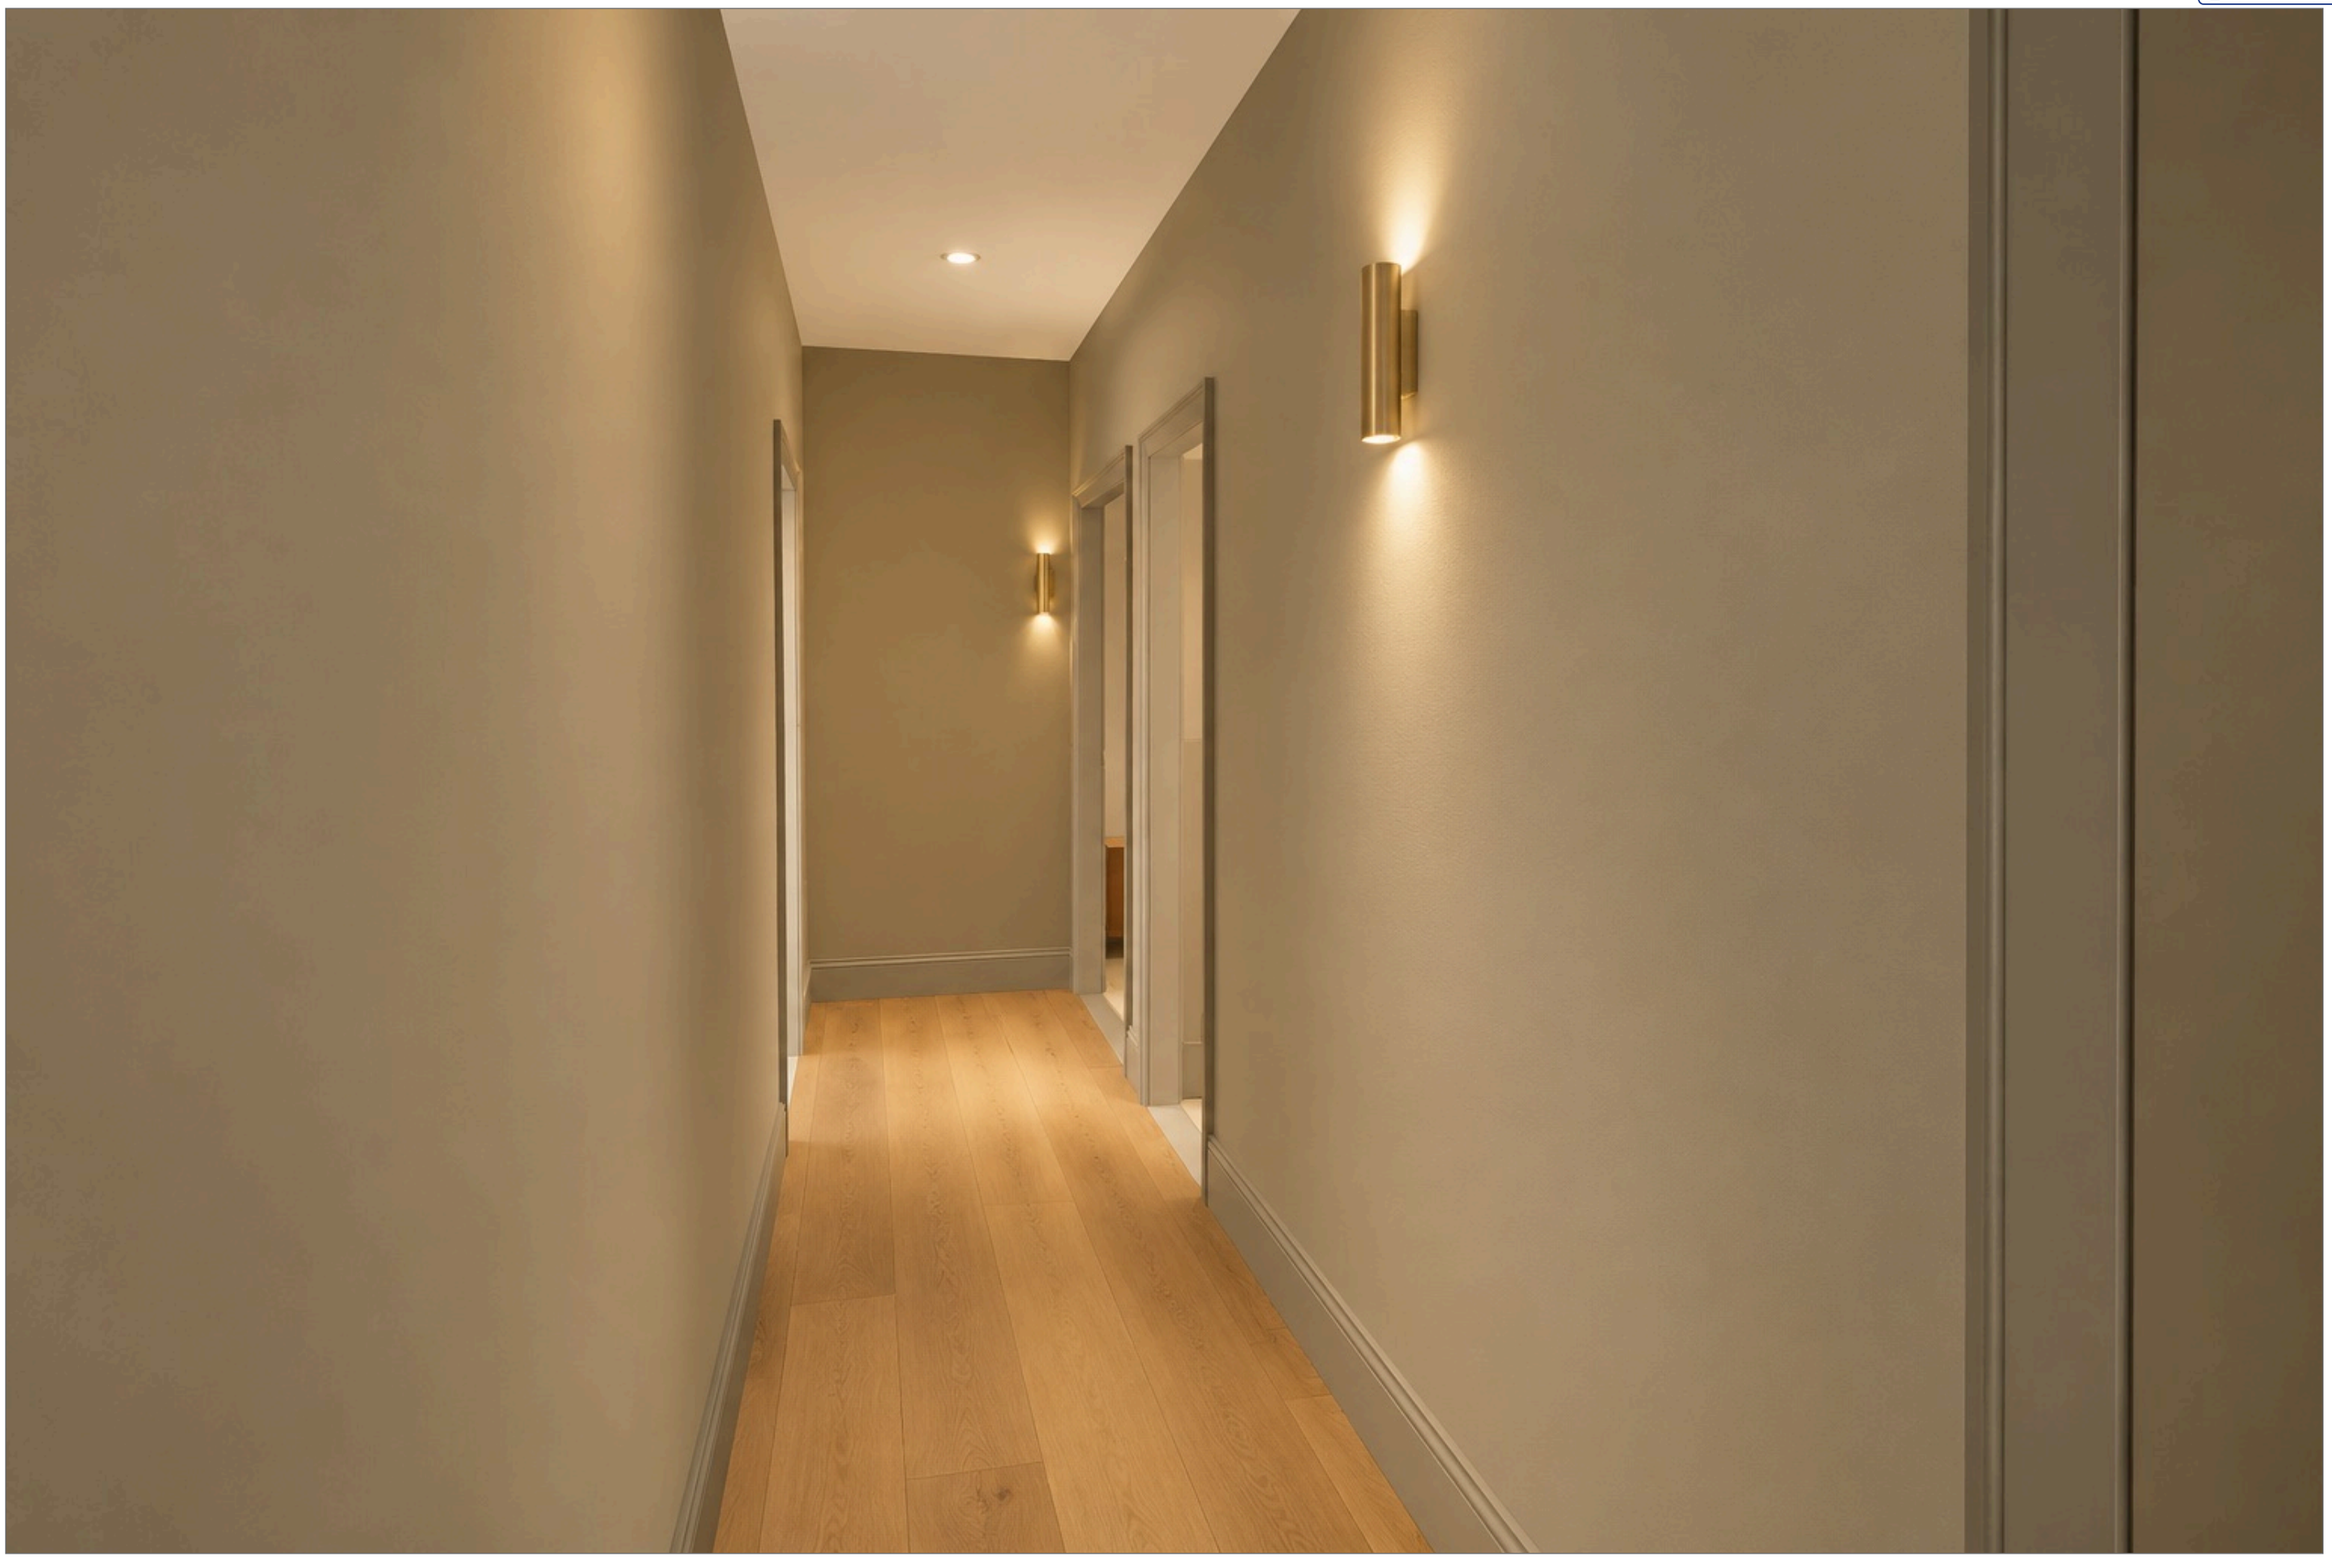

					Проект: Квартира с кабинетом	
	Лист	№ док.	Подпись	Дата		
Дизайнер	Кырлан А.С.			21.10.26	Визуализация коридора	Стадия / Лист / Листов
						П / 58 / 97

выпуск 18.10.2026 № 918b20bf25 · стр. 58 из 97

Правка к этому листу

Развёртка стены А1


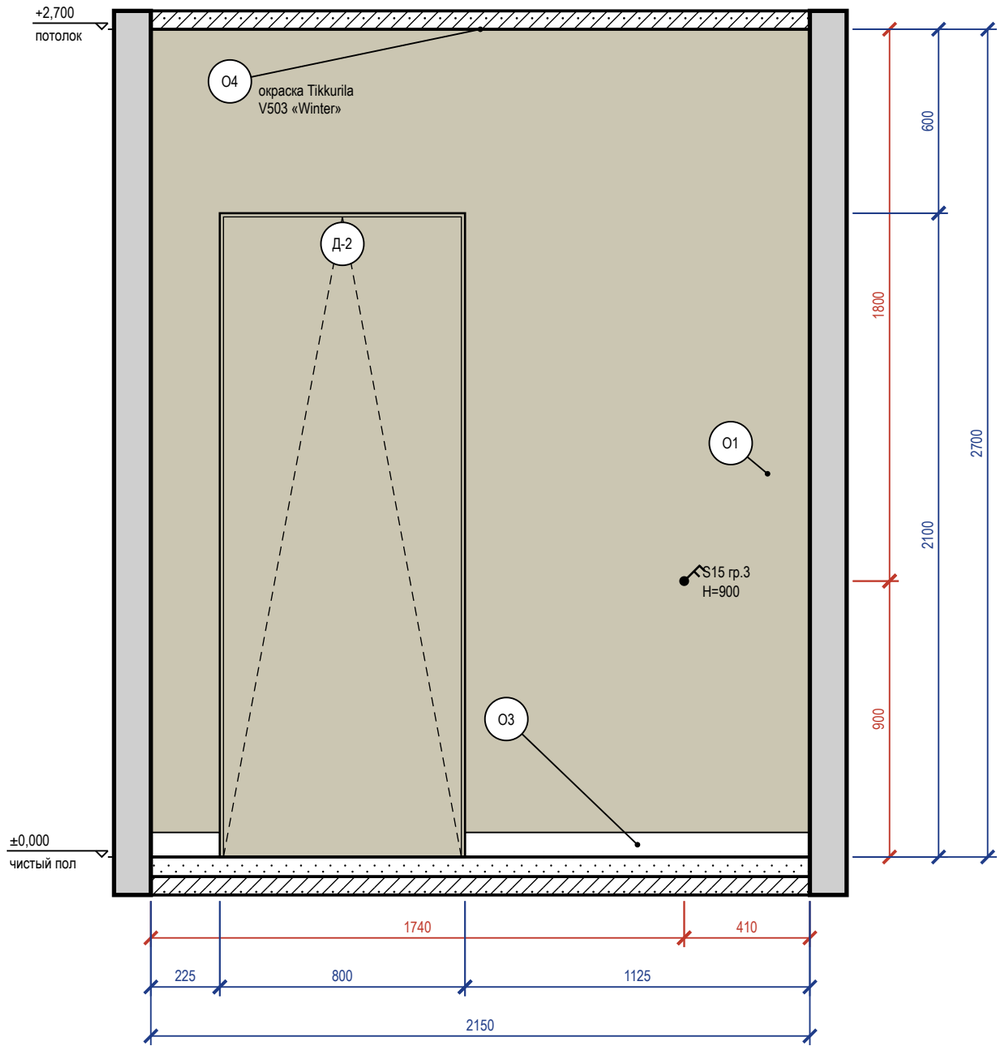


Схема развёрток (М 1:100)

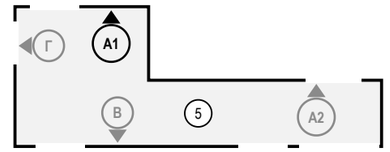


Ведомость отделки (на листе)

Марка	Поверхность	Материал, изделие	Цвет, код	Кол.
О1	стены	окраска, Farrow & Ball Modern Emulsion, матовая, подготовка Q3	Farrow & Ball No. 15 «Bone — мягкий каменно-серый с зеленцой»	4,1 м²
О3	плинтус	плинтус МДФ, h 80 мм, аналог: плинтус МДФ под покраску 80×16	Farrow & Ball No. 15 «Bone — мягкий каменно-серый с зеленцой»	1,4 м
О4	потолок	окраска, Tikkurila Anti-Reflex 2, глубокоматовая, подготовка Q3	Tikkurila V503 «Winter»	9,1 м²

2 Дверь скрытого монтажа в плоскости стены, плинтус (М 1:10)

Узел 2 — лист С3

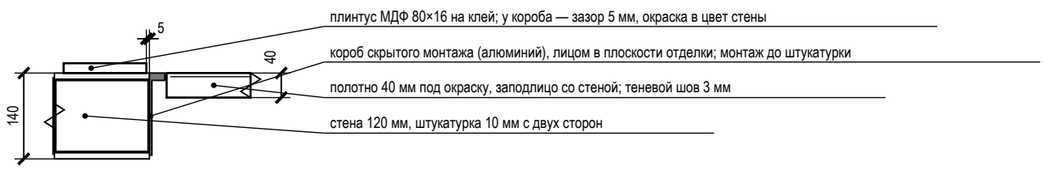

Примечания

1. Размеры — в мм от чистовых поверхностей стен; условные обозначения и общие указания — лист 2.
2. Двери скрытого монтажа — полотно в плоскости стены, отделка стены по полотну, плинтус прерывается у короба (узел — на листе узлов).

					Проект: Квартира с кабинетом
	Лист	№ док.	Подпись	Дата	
Дизайнер	Кырлан А.С.			21.10.26	Развёртка стены А1. Коридор (пом. 5)

Стадия	Лист	Листов
П	59	97

выпуск 18.10.2026 № 918b20bf25 · стр. 59 из 97

Правка к этому листу

Развёртка стены А2


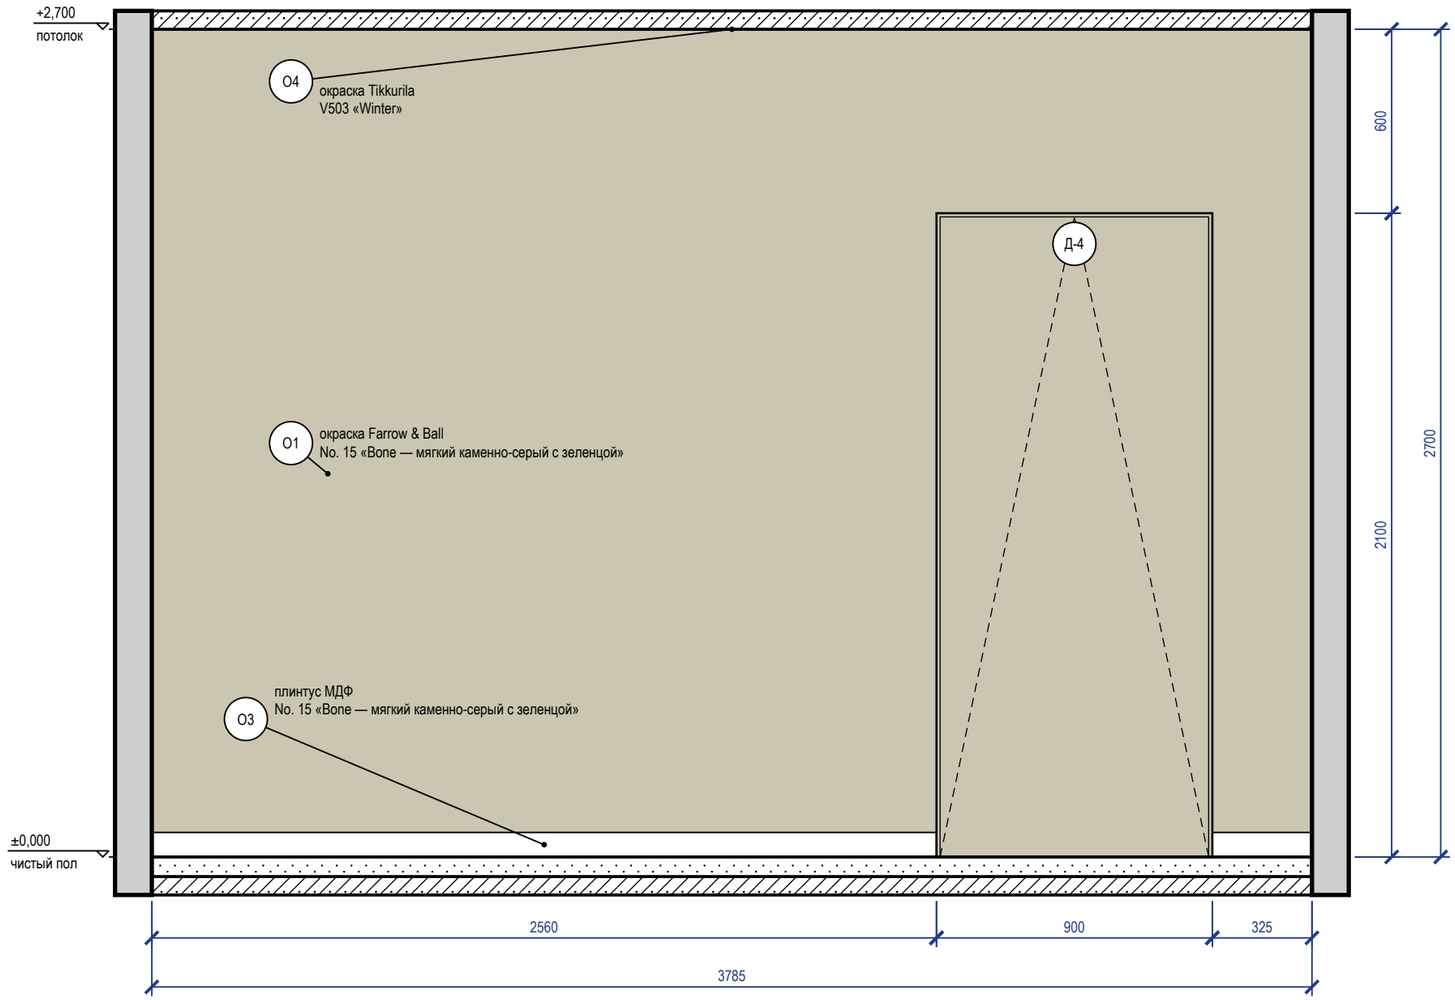


Схема развёрток (М 1:100)

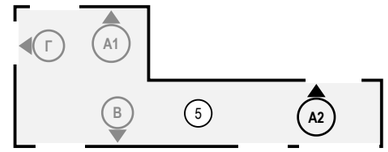

Ведомость отделки (на листе)

Марка	Поверхность	Материал, изделие	Цвет, код	Кол.
О1	стены	окраска, Farrow & Ball Modern Emulsion, матовая, подготовка Q3	Farrow & Ball No. 15 «Bone — мягкий каменно-серый с зеленцой»	8,3 м²
О3	плинтус	плинтус МДФ, h 80 мм, аналог: плинтус МДФ под покраску 80×16	Farrow & Ball No. 15 «Bone — мягкий каменно-серый с зеленцой»	2,9 м
О4	потолок	окраска, Tikkurila Anti-Reflex 2, глубокоматовая, подготовка Q3	Tikkurila V503 «Winter»	9,1 м²

Примечания

1. Размеры — в мм от чистовых поверхностей стен; условные обозначения и общие указания — лист 2.
2. Двери скрытого монтажа — полотно в плоскости стены, отделка стены по полотну, плинтус прерывается у короба (узел — на листе узлов).

	Лист	№ док.	Подпись	Дата
Дизайнер	Кырлан А.С.			21.10.26

Проект: Квартира с кабинетом

Развёртка стены А2. Коридор (пом. 5)

Стадия	Лист	Листов
П	60	97

выпуск 18.10.2026 № 918b20bf25 · стр. 60 из 97

Правка к этому листу

Развёртка стены В


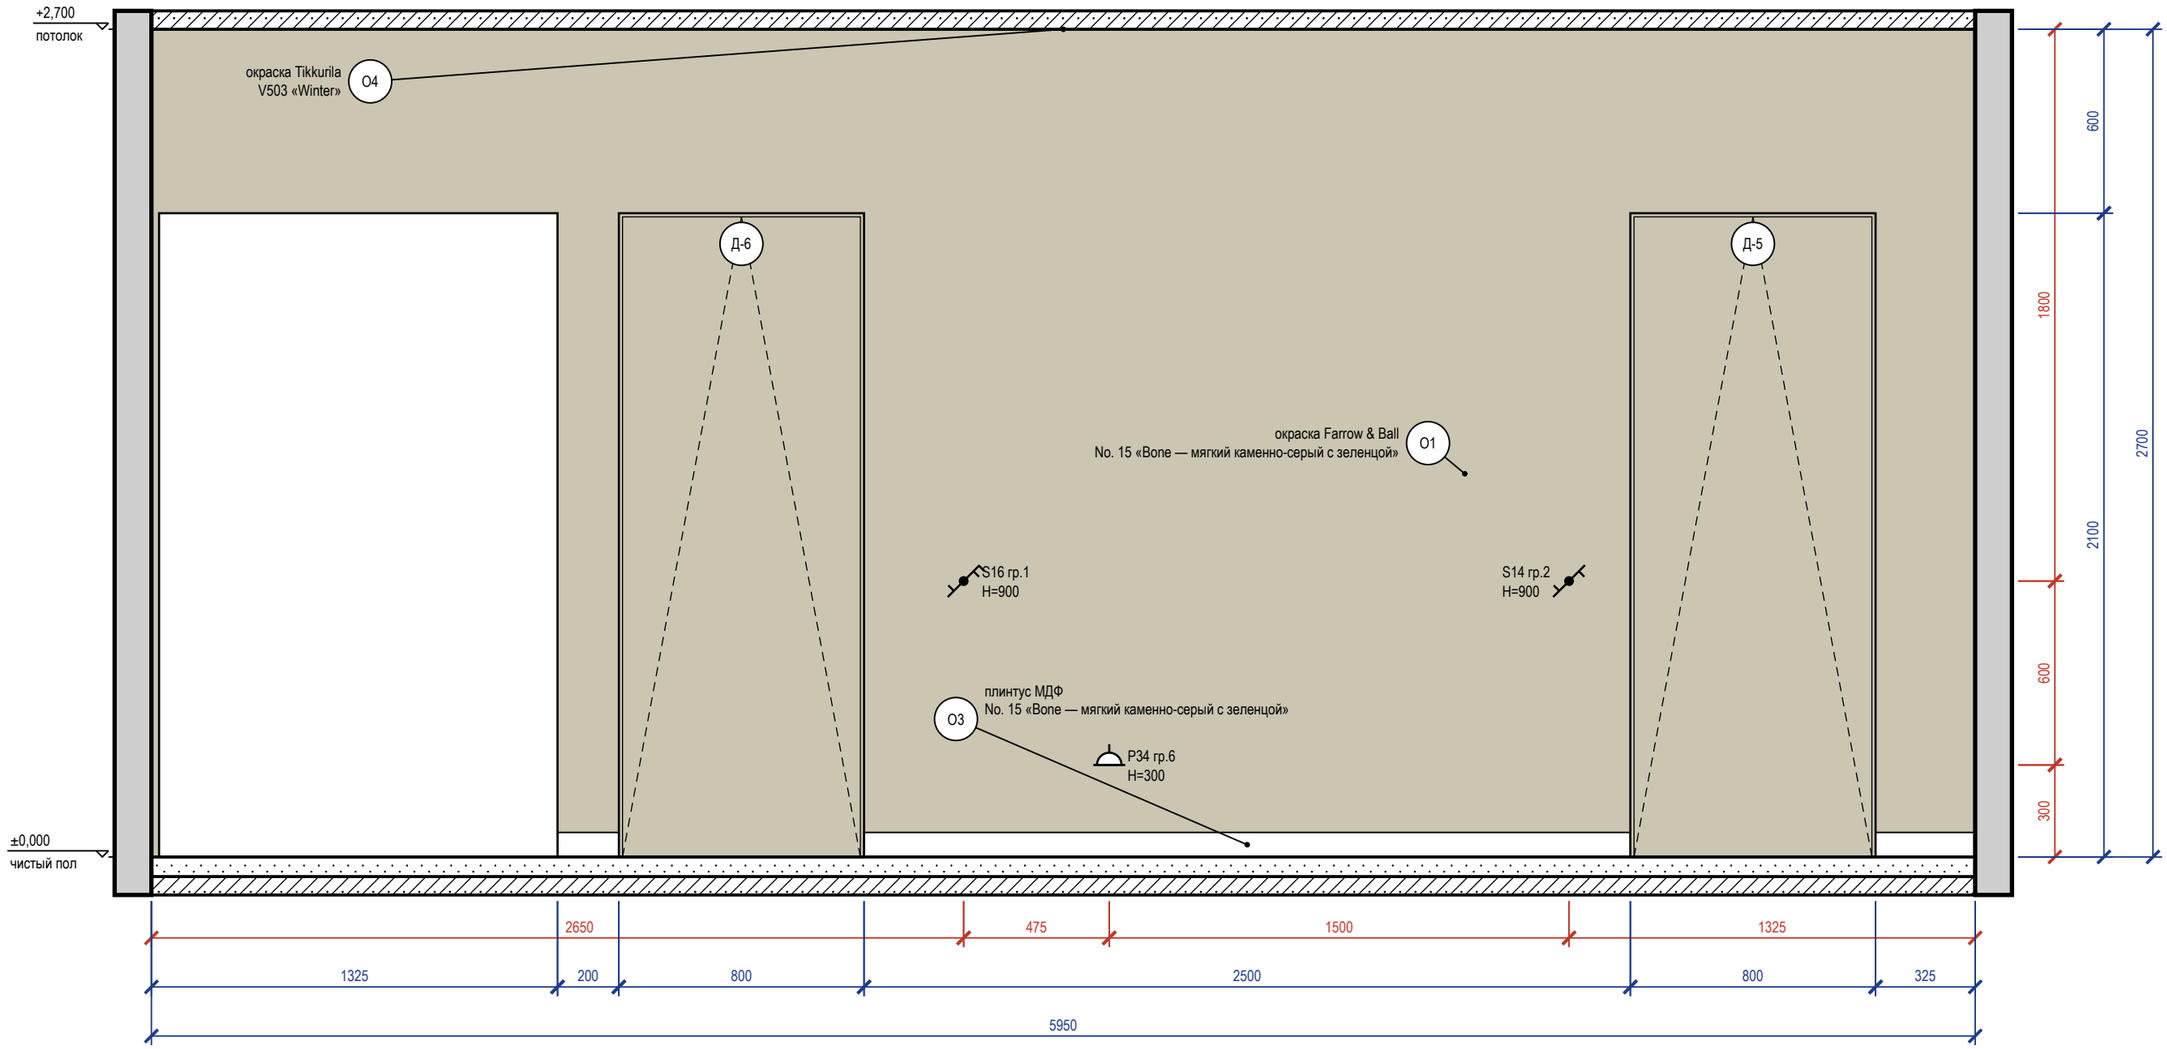



Схема развёрток (М 1:100)

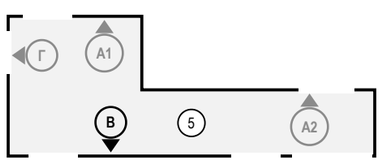

Ведомость отделки (на листе)

Марка	Поверхность	Материал, изделие	Цвет, код	Кол.
О1	стены	окраска, Farrow & Ball Modern Emulsion, матовая, подготовка Q3	Farrow & Ball No. 15 «Bone — мягкий каменно-серый с зеленцой»	10 м²
О3	плинтус	плинтус МДФ, h 80 мм, аналог: плинтус МДФ под покраску 80×16	Farrow & Ball No. 15 «Bone — мягкий каменно-серый с зеленцой»	3 м
О4	потолок	окраска, Tikkurila Anti-Reflex 2, глубокоматовая, подготовка Q3	Tikkurila V503 «Winter»	9,1 м²

Визуализация этой стены — лист 58

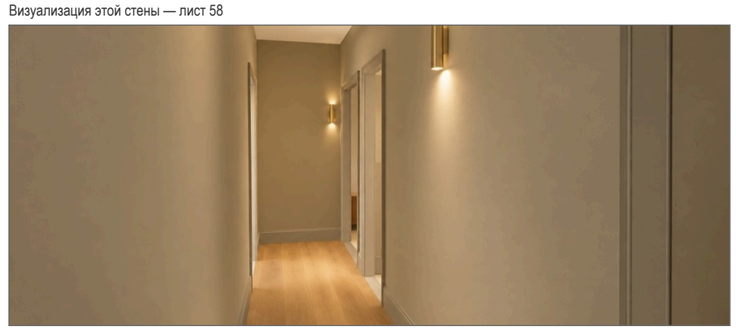

Примечания

1. Размеры — в мм от чистовых поверхностей стен; условные обозначения и общие указания — лист 2.
2. Двери скрытого монтажа — полотно в плоскости стены, отделка стены по полотну, плинтус прерывается у короба (узел — на листе узлов).

	Лист	№ док.	Подпись	Дата
Дизайнер	Кырлан А.С.			21.10.26

Проект: Квартира с кабинетом

Развёртка стены В. Коридор (пом. 5)

Стадия	Лист	Листов
П	61	97

выпуск 18.10.2026 № 918b20bf25 · стр. 61 из 97

Правка к этому листу

Развёртка стены Г


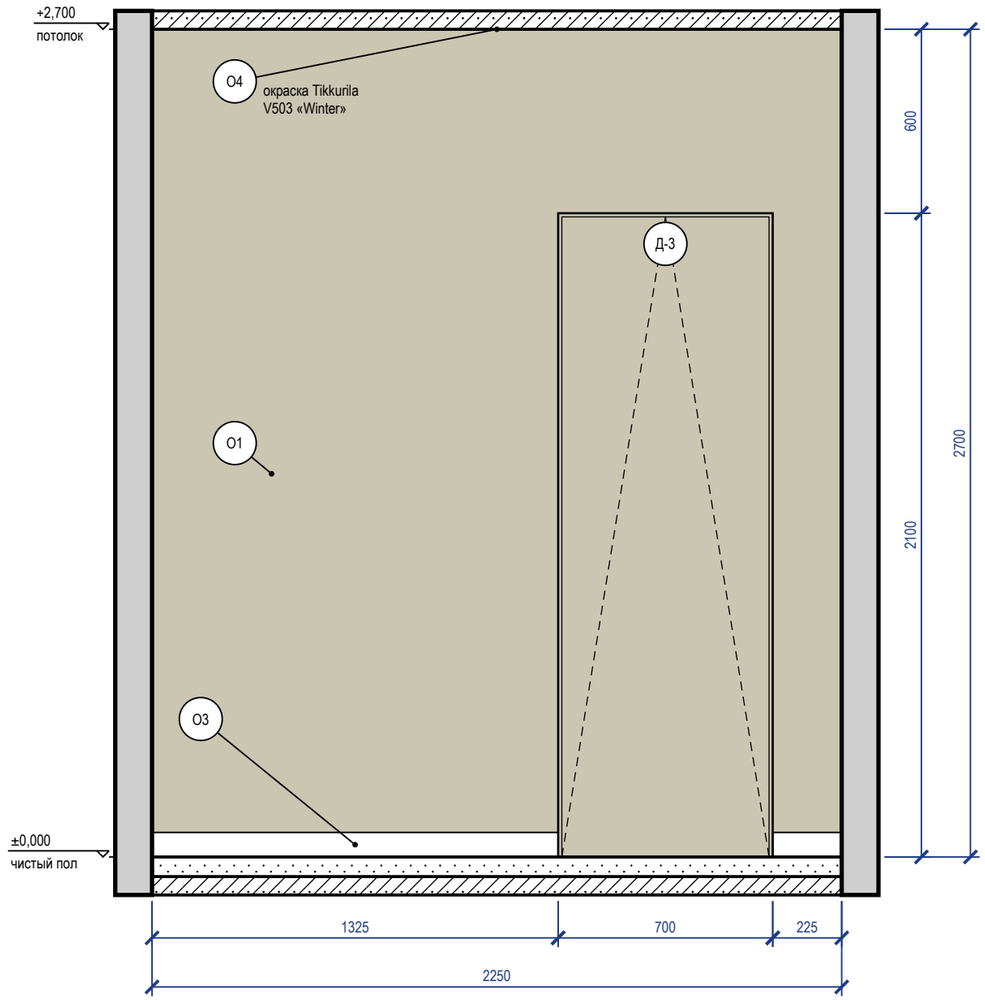


Схема развёрток (М 1:100)

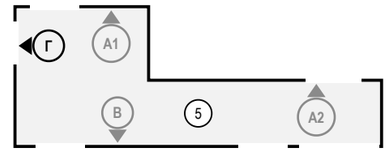

Ведомость отделки (на листе)

Марка	Поверхность	Материал, изделие	Цвет, код	Кол.
О1	стены	окраска, Farrow & Ball Modern Emulsion, матовая, подготовка Q3	Farrow & Ball No. 15 «Bone — мягкий каменно-серый с зеленцой»	4,6 м²
О3	плинтус	плинтус МДФ, h 80 мм, аналог: плинтус МДФ под покраску 80×16	Farrow & Ball No. 15 «Bone — мягкий каменно-серый с зеленцой»	1,6 м
О4	потолок	окраска, Tikkurila Anti-Reflex 2, глубокоматовая, подготовка Q3	Tikkurila V503 «Winter»	9,1 м²

Примечания

1. Размеры — в мм от чистовых поверхностей стен; условные обозначения и общие указания — лист 2.
2. Двери скрытого монтажа — полотно в плоскости стены, отделка стены по полотну, плинтус прерывается у короба (узел — на листе узлов).

					Проект: Квартира с кабинетом
	Лист	№ док.	Подпись	Дата	
Дизайнер	Кырлан А.С.			21.10.26	Развёртка стены Г. Коридор (пом. 5)

Стадия	Лист	Листов
П	62	97

выпуск 18.10.2026 № 918b20bf25 · стр. 62 из 97

Правка к этому листу



					Проект: Квартира с кабинетом
	Лист	№ док.	Подпись	Дата	
Дизайнер	Кырлан А.С.			21.10.26	Визуализация детской

Стадия	Лист	Листов
П	63	97

выпуск 18.10.2026 № 918b20bf25 · стр. 63 из 97

Правка к этому листу



					Проект: Квартира с кабинетом
	Лист	№ док.	Подпись	Дата	
Дизайнер	Кырлан А.С.			21.10.26	Визуализация детской

Стадия	Лист	Листов
П	64	97

выпуск 18.10.2026 № 918b20bf25 · стр. 64 из 97

Правка к этому листу



					Проект: Квартира с кабинетом
	Лист	№ док.	Подпись	Дата	
Дизайнер	Кырлан А.С.			21.10.26	Визуализация детской

Стадия	Лист	Листов
П	65	97

выпуск 18.10.2026 № 918b20bf25 · стр. 65 из 97

Правка к этому листу

Развёртка стены А


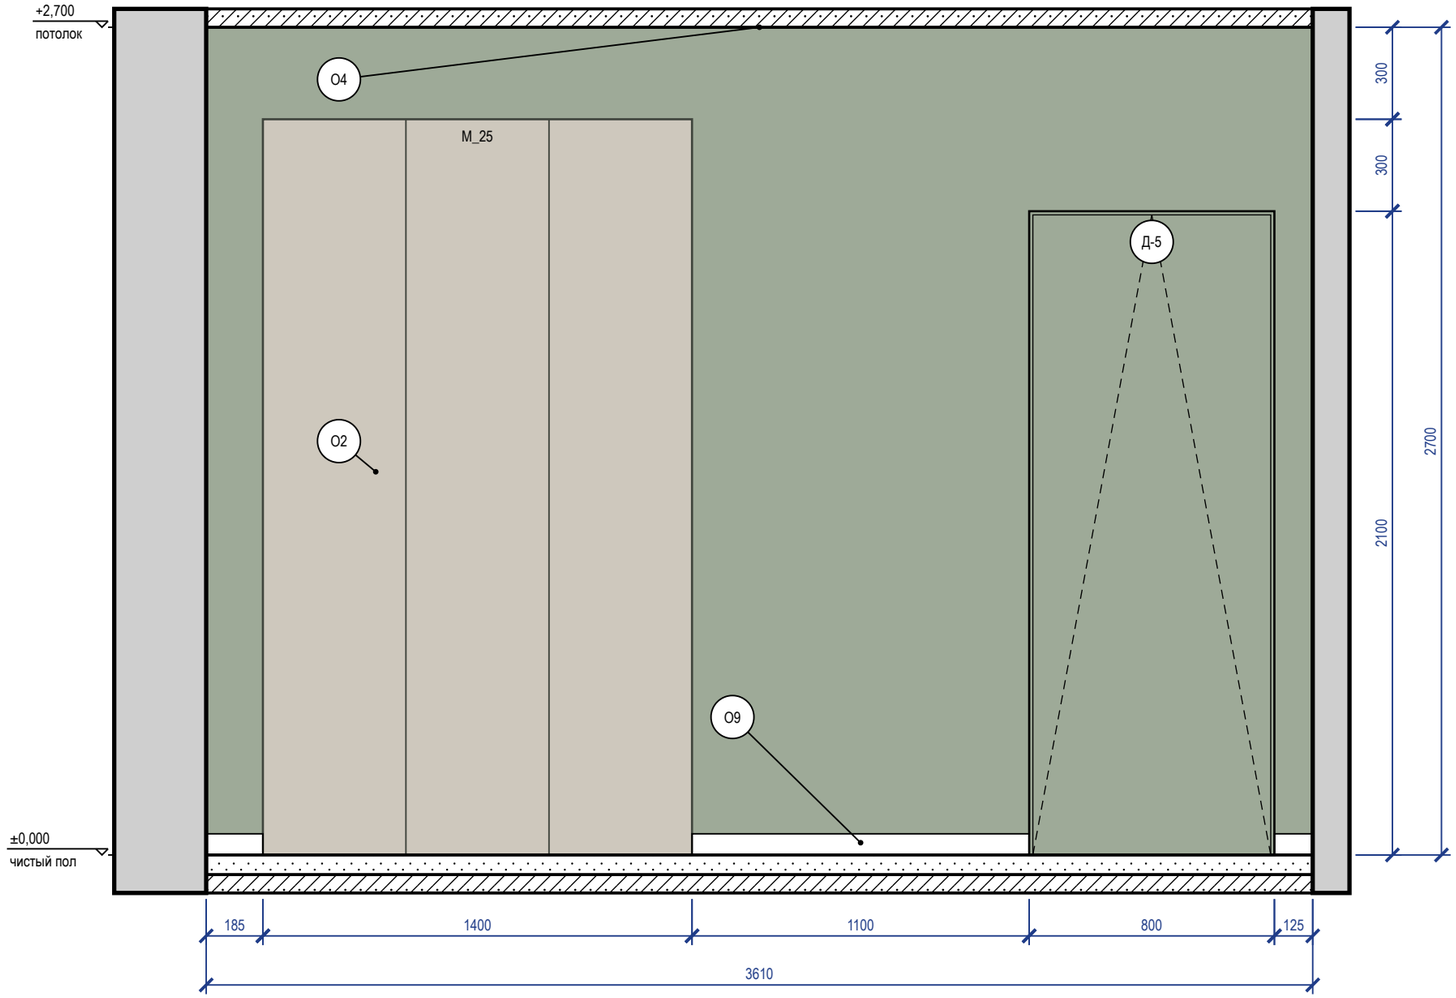


Схема развёрток (М 1:100)

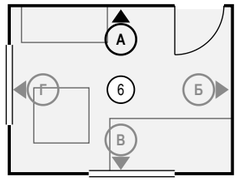

Ведомость отделки (на листе)

Марка	Поверхность	Материал, изделие	Цвет, код	Кол.
О2	акцентная стена	окраска, Farrow & Ball Modern Emulsion, матовая, подготовка Q3	Farrow & Ball No. 34 «Calke Green традиционный шалфей»	8,1 м²
О4	потолок	окраска, Tikkurila Anti-Reflex 2, глубокоматовая, подготовка Q3	Tikkurila V503 «Winter»	10 м²
О9	плинтус	плинтус МДФ, Orac Decor Contour (Luxxus), h 69 мм, SX165	Farrow & Ball No. 15 «Bone — мягкий каменно-серый с зеленцой»	1,4 м

Визуализация этой стены — лист 63



Примечания

1. Размеры — в мм от чистовых поверхностей стен; условные обозначения и общие указания — лист 2.
2. Двери скрытого монтажа — полотно в плоскости стены, отделка стены по полотну, плинтус прерывается у короба (узел — на листе узлов).

					Проект: Квартира с кабинетом
	Лист	№ док.	Подпись	Дата	Развёртка стены А. Детская (пом. 6)
Дизайнер	Кырлан А.С.			21.10.26	

Стадия	Лист	Листов
П	66	97

выпуск 18.10.2026 № 918b20bf25 · стр. 66 из 97

Правка к этому листу

Развёртка стены Б


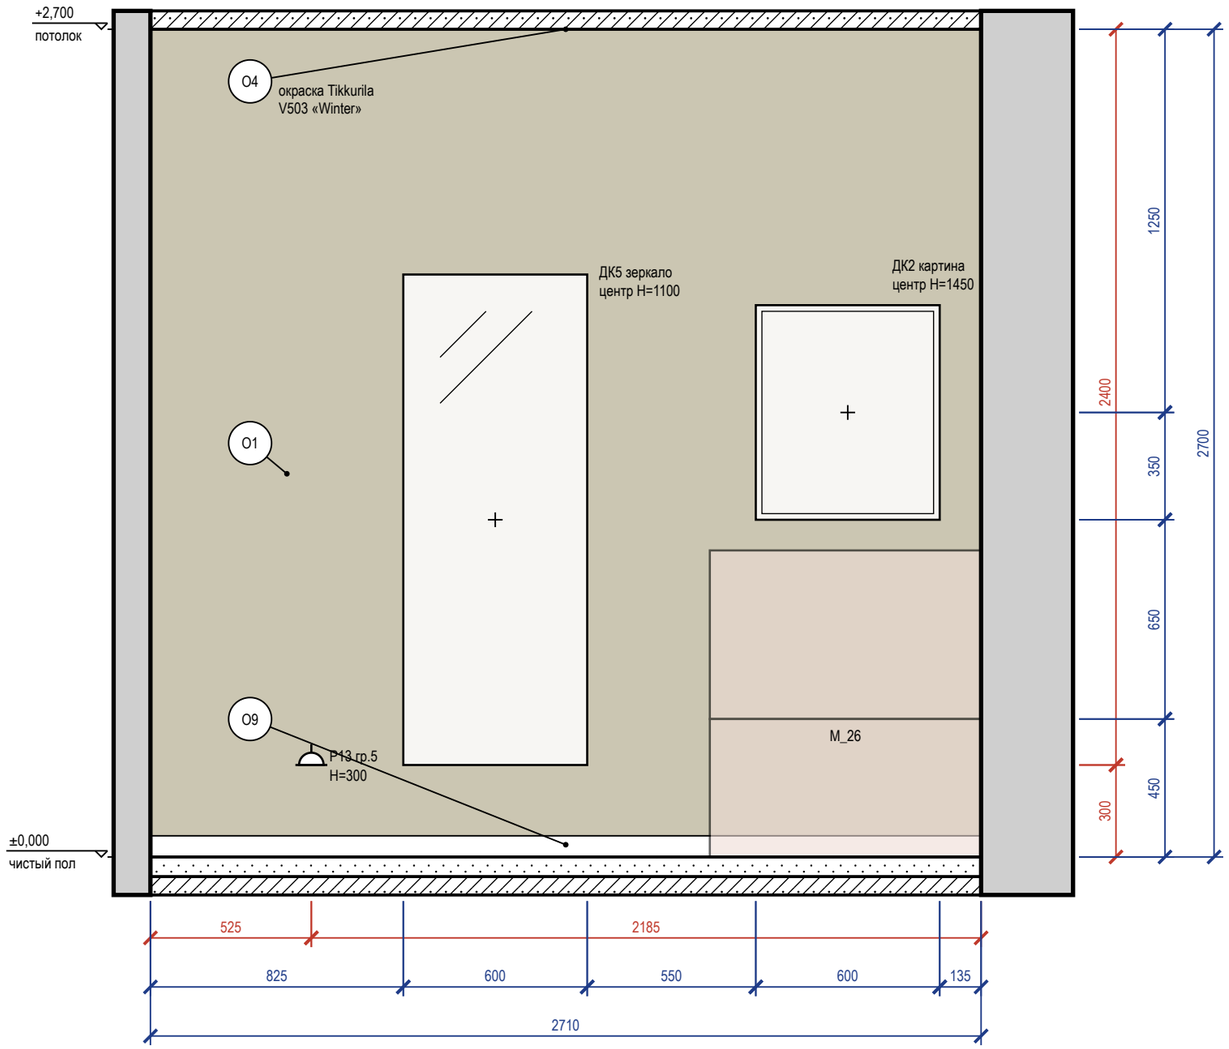


Схема развёрток (М 1:100)

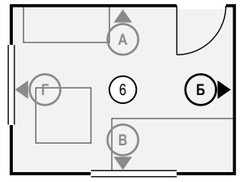

Ведомость отделки (на листе)

Марка	Поверхность	Материал, изделие	Цвет, код	Кол.
О1	стены	окраска, Farrow & Ball Modern Emulsion, матовая, подготовка Q3	Farrow & Ball No. 15 «Bone — мягкий каменно-серый с зеленцой»	7,3 м²
О4	потолок	окраска, Tikkurila Anti-Reflex 2, глубокоматовая, подготовка Q3	Tikkurila V503 «Winter»	10 м²
О9	плинтус	плинтус МДФ, Orac Decor Contour (Luxxus), h 69 мм, SX165	Farrow & Ball No. 15 «Bone — мягкий каменно-серый с зеленцой»	2,7 м

Визуализация этой стены — лист 64



Примечания

1. Размеры — в мм от чистовых поверхностей стен; условные обозначения и общие указания — лист 2.
2. Картины и зеркала крепить к основанию по паспорту изделия (закладные и анкеры — в перечне скрытых работ); крест — ось центра предмета.

	Лист	№ док.	Подпись	Дата
Дизайнер	Кырлан А.С.			21.10.26

Проект: Квартира с кабинетом

Развёртка стены Б. Детская (пом. 6)

Стадия	Лист	Листов
П	67	97

выпуск 18.10.2026 № 918b20bf25 · стр. 67 из 97

Правка к этому листу

Развёртка стены В


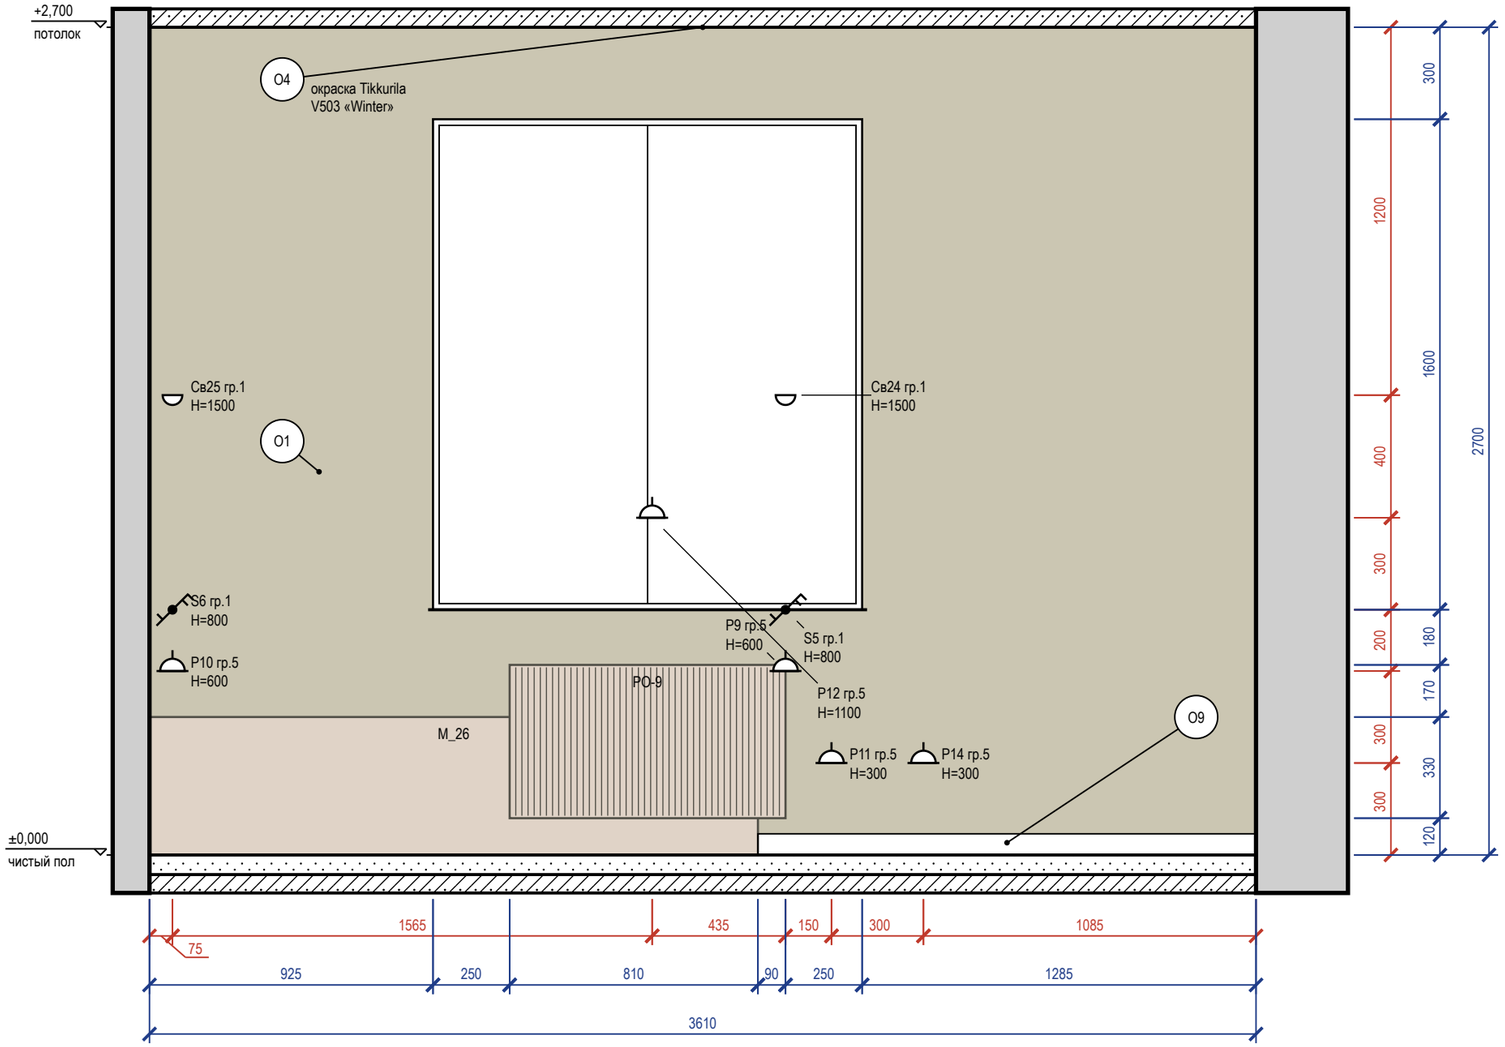


Схема развёрток (М 1:100)

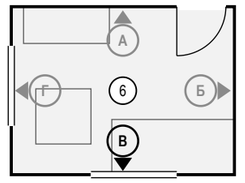

Ведомость отделки (на листе)

Марка	Поверхность	Материал, изделие	Цвет, код	Кол.
О1	стены	окраска, Farrow & Ball Modern Emulsion, матовая, подготовка Q3	Farrow & Ball No. 15 «Bone — мягкий каменно-серый с зеленцой»	7,5 м²
О4	потолок	окраска, Tikkurila Anti-Reflex 2, глубокоматовая, подготовка Q3	Tikkurila V503 «Winter»	10 м²
О9	плинтус	плинтус МДФ, Orac Decor Contour (Luxxus), h 69 мм, SX165	Farrow & Ball No. 15 «Bone — мягкий каменно-серый с зеленцой»	1,6 м

Примечания

1. Размеры — в мм от чистовых поверхностей стен; условные обозначения и общие указания — лист 2.

					Проект: Квартира с кабинетом
	Лист	№ док.	Подпись	Дата	Развёртка стены В. Детская (пом. 6)
Дизайнер	Кырлан А.С.			21.10.26	

Стадия	Лист	Листов
П	68	97

выпуск 18.10.2026 № 918b20bf25 · стр. 68 из 97

Правка к этому листу

Развёртка стены Г


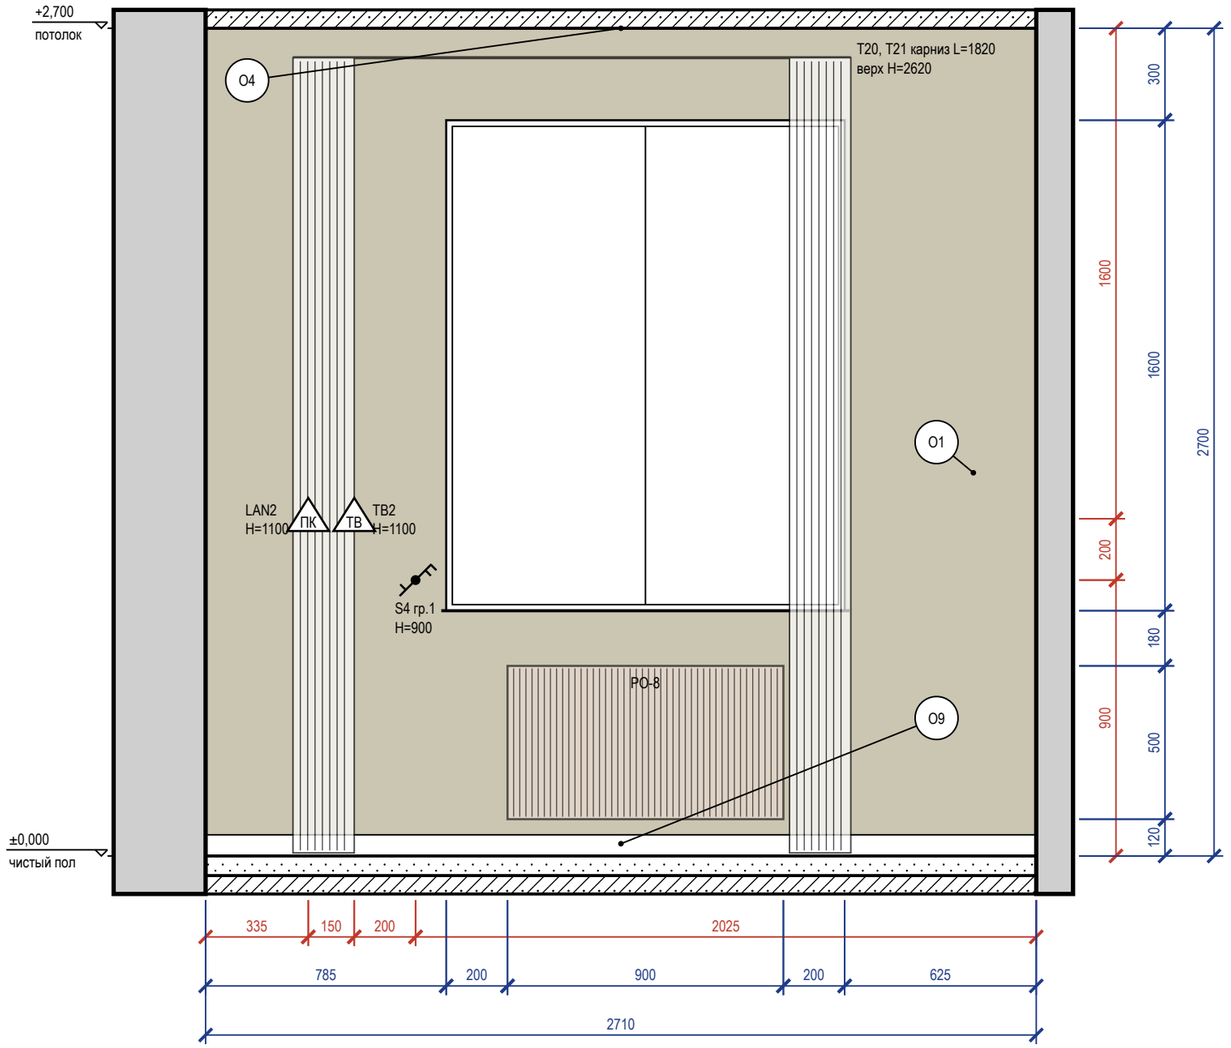


Схема развёрток (М 1:100)

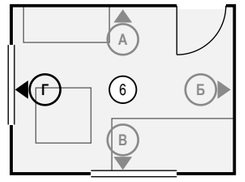

Ведомость отделки (на листе)

Марка	Поверхность	Материал, изделие	Цвет, код	Кол.
О1	стены	окраска, Farrow & Ball Modern Emulsion, матовая, подготовка Q3	Farrow & Ball No. 15 «Bone — мягкий каменно-серый с зеленцой»	5,2 м²
О4	потолок	окраска, Tikkurila Anti-Reflex 2, глубокоматовая, подготовка Q3	Tikkurila V503 «Winter»	10 м²
О9	плинтус	плинтус МДФ, Orac Decor Contour (Luxxus), h 69 мм, SX165	Farrow & Ball No. 15 «Bone — мягкий каменно-серый с зеленцой»	2,7 м

Визуализация этой стены — лист 65



Примечания

1. Размеры — в мм от чистовых поверхностей стен; условные обозначения и общие указания — лист 2.
2. Карнизы (шины) — по ведомости текстиля декоратора; длина L и верх H — по развёртке, крепление — до окраски потолка.

					Проект: Квартира с кабинетом
	Лист	№ док.	Подпись	Дата	Развёртка стены Г. Детская (пом. 6)
Дизайнер	Кырлан А.С.			21.10.26	

Стадия	Лист	Листов
П	69	97

выпуск 18.10.2026 № 918b20bf25 · стр. 69 из 97

Правка к этому листу



					Проект: Квартира с кабинетом
	Лист	№ док.	Подпись	Дата	
Дизайнер	Кырлан А.С.			21.10.26	Визуализация ванной

Стадия	Лист	Листов
П	70	97

выпуск 18.10.2026 № 918b20bf25 · стр. 70 из 97

Правка к этому листу



					Проект: Квартира с кабинетом
	Лист	№ док.	Подпись	Дата	
Дизайнер	Кырлан А.С.			21.10.26	Визуализация ванной

Стадия	Лист	Листов
П	71	97

выпуск 18.10.2026 № 918b20bf25 · стр. 71 из 97

Правка к этому листу



					Проект: Квартира с кабинетом
	Лист	№ док.	Подпись	Дата	
Дизайнер	Кырлан А.С.			21.10.26	Визуализация ванной

Стадия	Лист	Листов
П	72	97

выпуск 18.10.2026 № 918b20bf25 · стр. 72 из 97

Правка к этому листу

Развёртка стены А


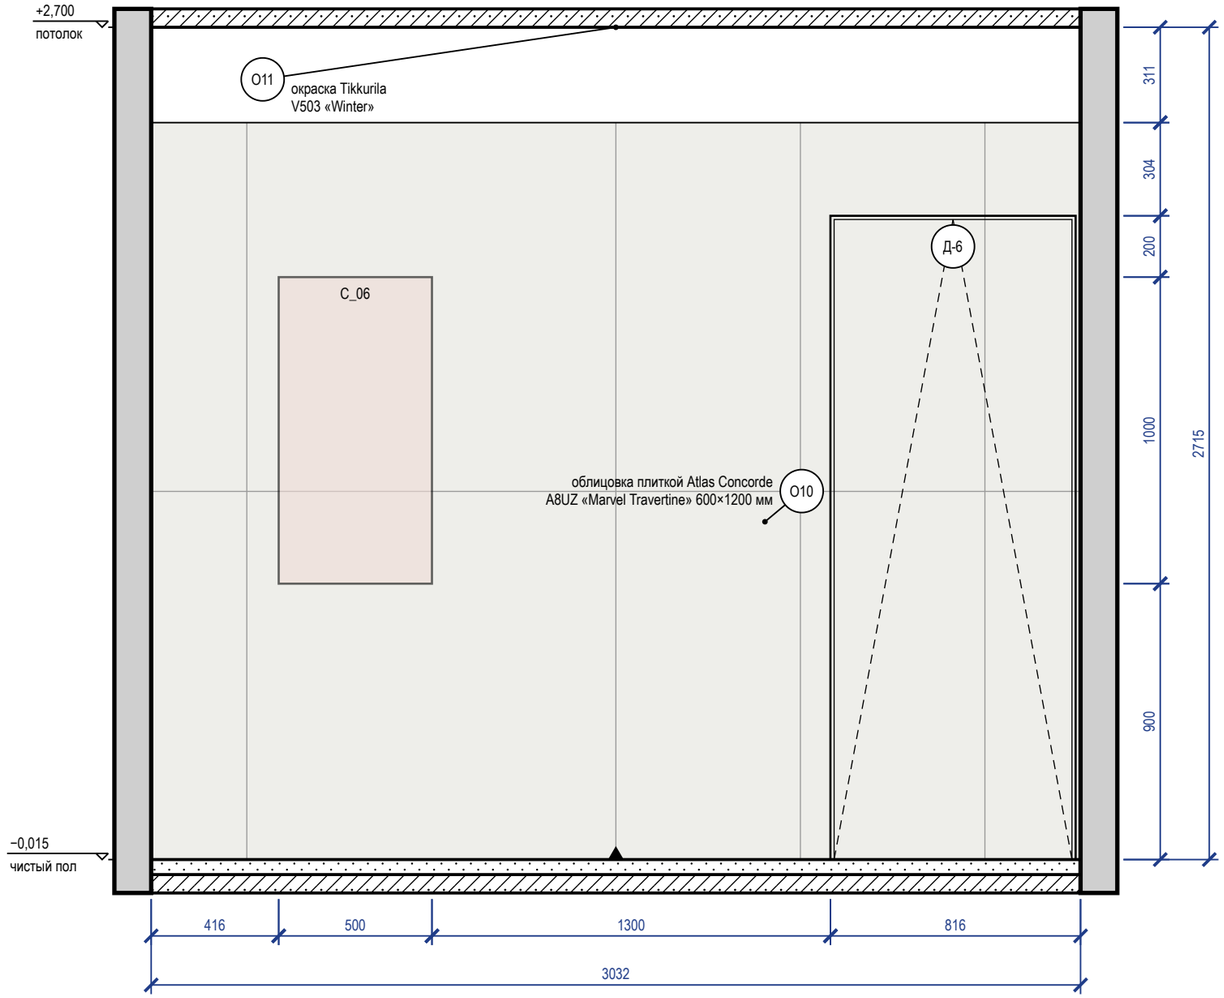



Схема развёрток (М 1:100)

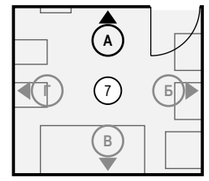

Ведомость отделки (на листе)

Марка	Поверхность	Материал, изделие	Цвет, код	Кол.
О10	стены	облицовка плиткой, Atlas Concorde Marvel Travertine, 600×1200×9 мм, А8UZ, затирка CG2WA	Atlas Concorde A8UZ «Marvel Travertine»	5,6 м²
О11	потолок	окраска, Tikkurila Luja 7, матовая, подготовка Q3	Tikkurila V503 «Winter»	8,4 м²

1 **Порог 15 мм: мокрая зона — жилое помещение (М 1:10)**
Узел 1 — лист С3

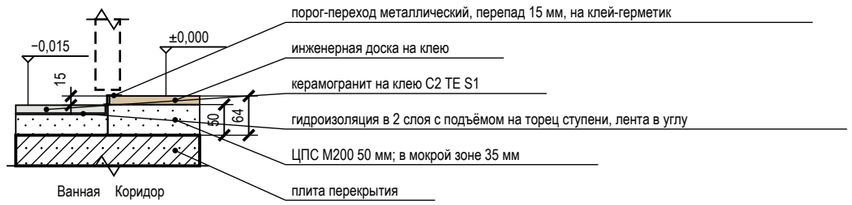

Примечания

1. Размеры — в мм от чистовых поверхностей стен; условные обозначения и общие указания — лист 2.
2. Облицовка — по сетке швов 2 мм, раскладка от оси стены (треугольник у пола), целые ряды от пола; подрезки — по листу раскладки плитки.
3. Гидроизоляция в 2 слоя, заход на стены 200 мм — до облицовки, с актом скрытых работ и тестом проливом (узел — на листе узлов).
4. Двери скрытого монтажа — полотно в плоскости стены, отделка стены по полотну, плинтус прерывается у короба (узел — на листе узлов).

					Проект: Квартира с кабинетом
	Лист	№ док.	Подпись	Дата	Разверстка стены А. Ванная (пом. 7)
Дизайнер	Кырлан А.С.			21.10.26	

Стадия	Лист	Листов
П	73	97

выпуск 18.10.2026 № 918b20bf25 · стр. 73 из 97

Правка к этому листу

Развёртка стены Б


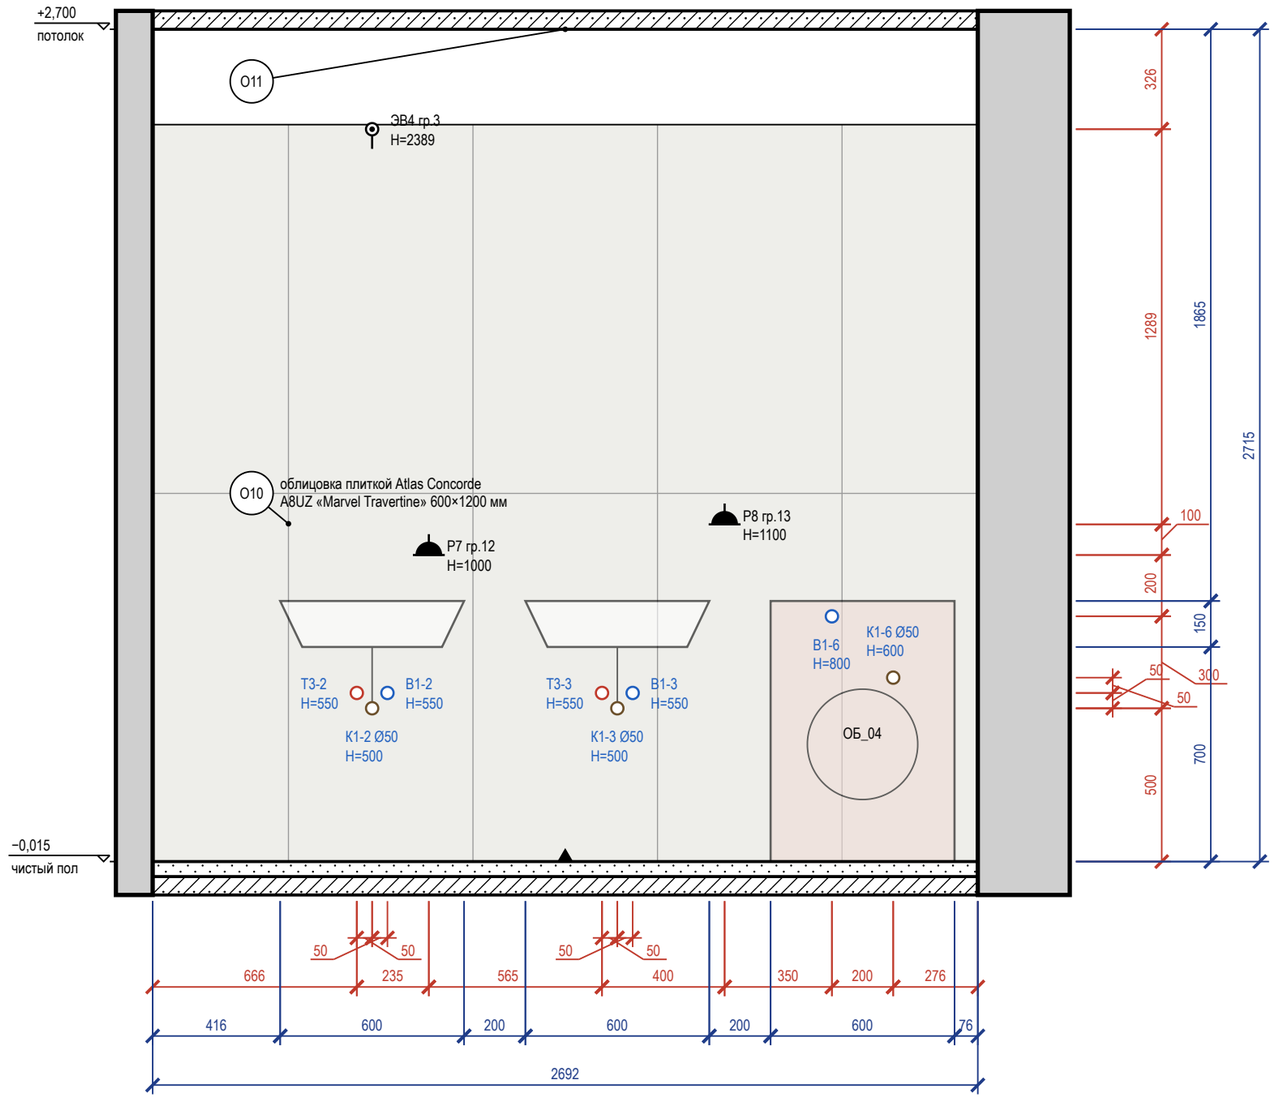


Схема развёрток (М 1:100)

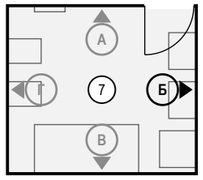

Ведомость отделки (на листе)

Марка	Поверхность	Материал, изделие	Цвет, код	Кол.
О10	стены	облицовка плиткой, Atlas Concorde Marvel Travertine, 600×1200×9 мм, A8UZ, затирка CG2WA	Atlas Concorde A8UZ «Marvel Travertine»	6,5 м²
О11	потолок	окраска, Tikkurila Luja 7, матовая, подготовка Q3	Tikkurila V503 «Winter»	8,4 м²

Визуализация этой стены — лист 70



Примечания

1. Размеры — в мм от чистовых поверхностей стен; условные обозначения и общие указания — лист 2.
2. Схема мебели, приборов и декора не является технической документацией для производства мебели; габариты — по паспортам изделий.
3. Облицовка — по сетке швов 2 мм, раскладка от оси стены (треугольник у пола), целые ряды от пола; подрезки — по листу раскладки плитки.
4. Гидроизоляция в 2 слоя, заход на стены 200 мм — до облицовки, с актом скрытых работ и тестом проливом (узел — на листе узлов).

					Проект: Квартира с кабинетом
	Лист	№ док.	Подпись	Дата	Развёртка стены Б. Ванная (пом. 7)
Дизайнер	Кырлан А.С.			21.10.26	

Стадия	Лист	Листов
П	74	97

выпуск 18.10.2026 № 918b20bf25 · стр. 74 из 97

Развёртка стены В


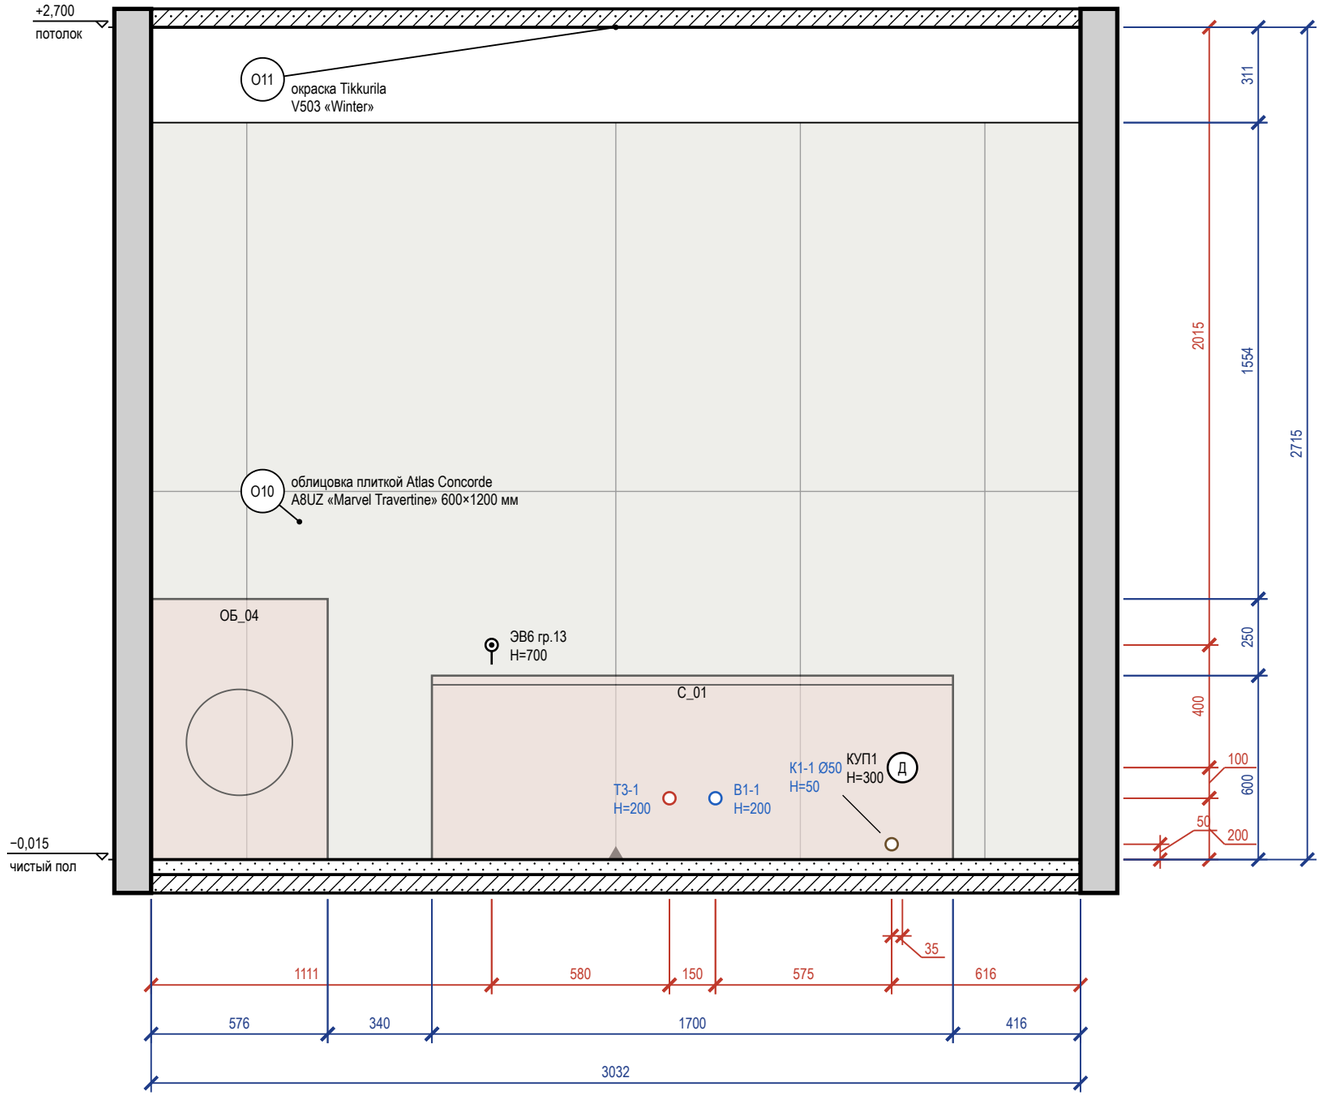


Схема развёрток (М 1:100)

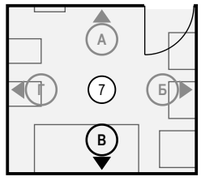

Ведомость отделки (на листе)

Марка	Поверхность	Материал, изделие	Цвет, код	Кол.
О10	стены	облицовка плиткой, Atlas Concorde Marvel Travertine, 600×1200×9 мм, A8UZ, затирка CG2WA	Atlas Concorde A8UZ «Marvel Travertine»	7,3 м²
О11	потолок	окраска, Tikkurila Luja 7, матовая, подготовка Q3	Tikkurila V503 «Winter»	8,4 м²

Визуализация этой стены — лист 71



Примечания

1. Размеры — в мм от чистовых поверхностей стен; условные обозначения и общие указания — лист 2.
2. Схема мебели, приборов и декора не является технической документацией для производства мебели; габариты — по паспортам изделий.
3. Облицовка — по сетке швов 2 мм, раскладка от оси стены (треугольник у пола), целые ряды от пола; подрезки — по листу раскладки плитки.
4. Гидроизоляция в 2 слоя, заход на стены 200 мм — до облицовки, с актом скрытых работ и тестом проливом (узел — на листе узлов).

					Проект: Квартира с кабинетом
	Лист	№ док.	Подпись	Дата	Развёртка стены В. Ванная (пом. 7)
Дизайнер	Кырлан А.С.			21.10.26	

Стадия	Лист	Листов
П	75	97

Правка к этому листу

Развёртка стены Г


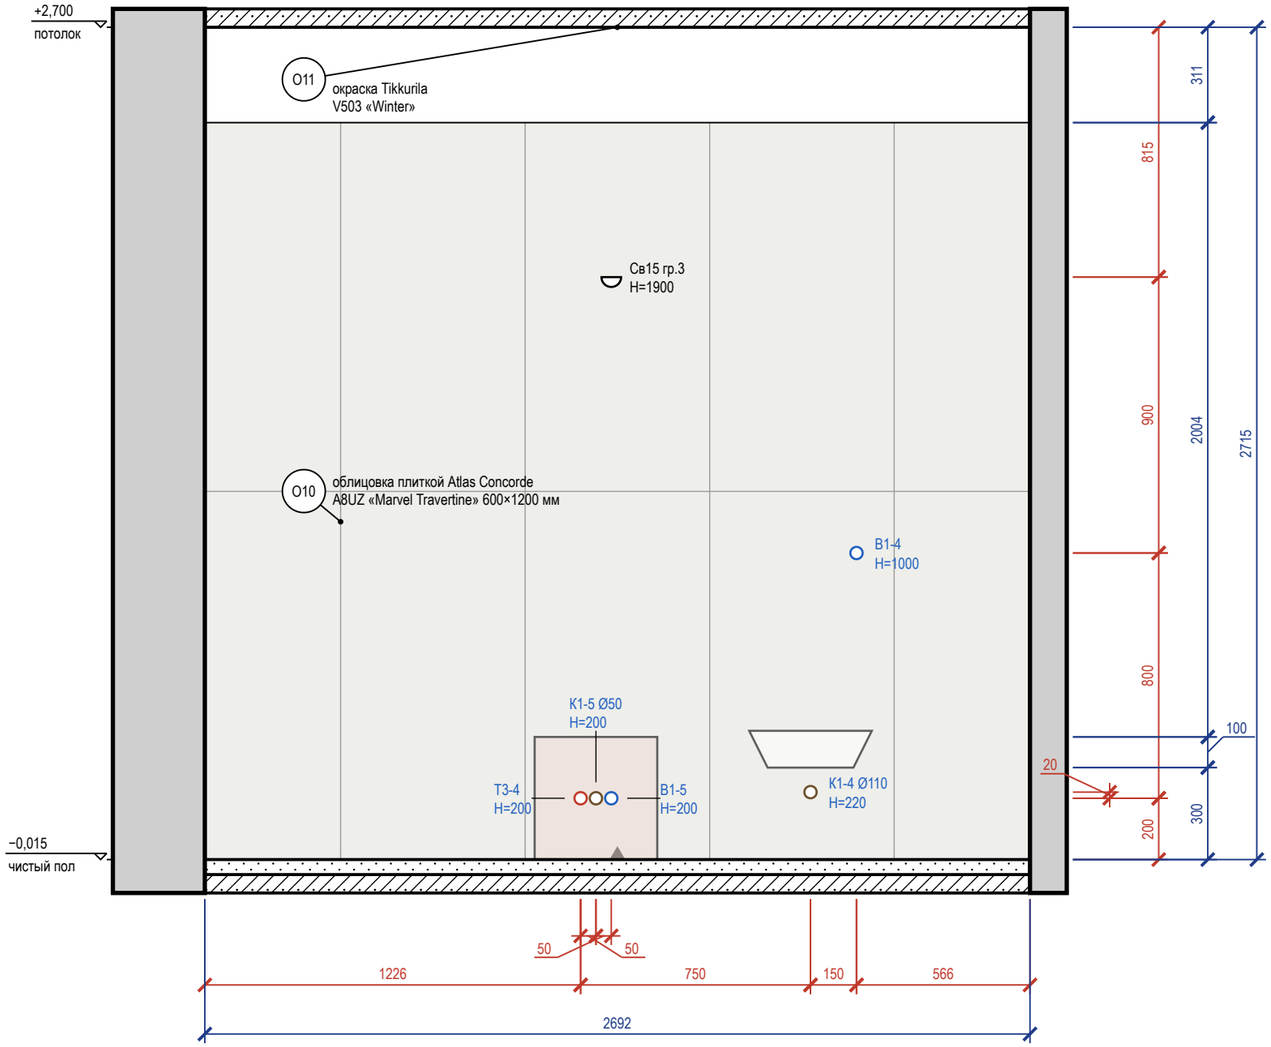


Схема развёрток (М 1:100)

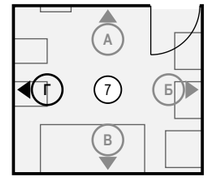

Ведомость отделки (на листе)

Марка	Поверхность	Материал, изделие	Цвет, код	Кол.
О10	стены	облицовка плиткой, Atlas Concorde Marvel Travertine, 600×1200×9 мм, A8UZ, затирка CG2WA	Atlas Concorde A8UZ «Marvel Travertine»	6,5 м²
О11	потолок	окраска, Tikkurila Luja 7, матовая, подготовка Q3	Tikkurila V503 «Winter»	8,4 м²

Визуализация этой стены — лист 72



Примечания

1. Размеры — в мм от чистовых поверхностей стен; условные обозначения и общие указания — лист 2.
2. Схема мебели, приборов и декора не является технической документацией для производства мебели; габариты — по паспортам изделий.
3. Облицовка — по сетке швов 2 мм, раскладка от оси стены (треугольник у пола), целые ряды от пола; подрезки — по листу раскладки плитки.
4. Гидроизоляция в 2 слоя, заход на стены 200 мм — до облицовки, с актом скрытых работ и тестом проливом (узел — на листе узлов).

					Проект: Квартира с кабинетом
	Лист	№ док.	Подпись	Дата	Развёртка стены Г. Ванная (пом. 7)
Дизайнер	Кырлан А.С.			21.10.26	

Стадия	Лист	Листов
П	76	97

выпуск 18.10.2026 № 918b20bf25 · стр. 76 из 97

Правка к этому листу



					Проект: Квартира с кабинетом	
	Лист	№ док.	Подпись	Дата		
Дизайнер	Кырлан А.С.			21.10.26	Визуализация прихожей	Стадия / Лист / Листов
						П / 77 / 97

выпуск 18.10.2026 № 918b20bf25 · стр. 77 из 97

Правка к этому листу



					Проект: Квартира с кабинетом
	Лист	№ док.	Подпись	Дата	
Дизайнер	Кырлан А.С.			21.10.26	Визуализация прихожей
					Стадия: П; Лист: 78; Листов: 97

выпуск 18.10.2026 № 918b20bf25 · стр. 78 из 97

Правка к этому листу



					Проект: Квартира с кабинетом
	Лист	№ док.	Подпись	Дата	
Дизайнер	Кырлан А.С.			21.10.26	Визуализация прихожей

Стадия	Лист	Листов
П	79	97

выпуск 18.10.2026 № 918b20bf25 · стр. 79 из 97

Правка к этому листу

Развёртка стены Б


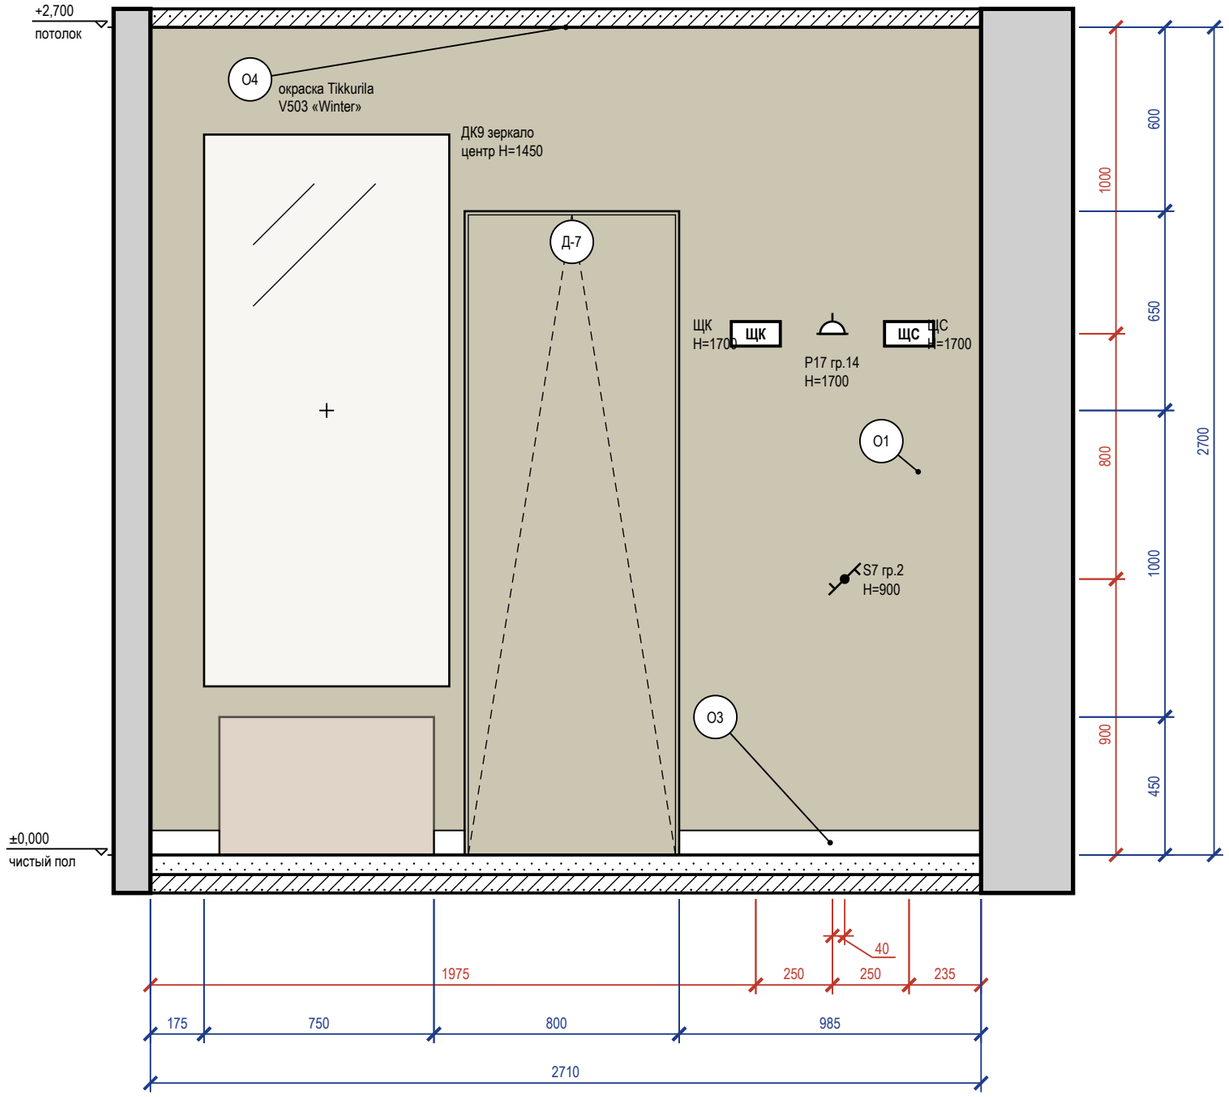


Схема развёрток (М 1:100)

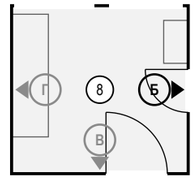

Ведомость отделки (на листе)

Марка	Поверхность	Материал, изделие	Цвет, код	Кол.
О1	стены	окраска, Farrow & Ball Modern Emulsion, матовая, подготовка Q3	Farrow & Ball No. 15 «Bone — мягкий каменно-серый с зеленцой»	5,8 м²
О3	плинтус	плинтус МДФ, h 80 мм, аналог: плинтус МДФ под покраску 80×16	Farrow & Ball No. 15 «Bone — мягкий каменно-серый с зеленцой»	1,3 м
О4	потолок	окраска, Tikkurila Anti-Reflex 2, глубокоматовая, подготовка Q3	Tikkurila V503 «Winter»	7,9 м²

Визуализация этой стены — лист 77



Примечания

1. Размеры — в мм от чистовых поверхностей стен; условные обозначения и общие указания — лист 2.
2. Картины и зеркала крепить к основанию по паспорту изделия (закладные и анкеры — в перечне скрытых работ); крест — ось центра предмета.
3. Двери скрытого монтажа — полотно в плоскости стены, отделка стены по полотну, плинтус прерывается у короба (узел — на листе узлов).

					Проект: Квартира с кабинетом
	Лист	№ док.	Подпись	Дата	Развёртка стены Б. Прихожая (пом. 8)
Дизайнер	Кырлан А.С.			21.10.26	

Стадия	Лист	Листов
П	80	97

выпуск 18.10.2026 № 918b20bf25 · стр. 80 из 97

Правка к этому листу

Развёртка стены В


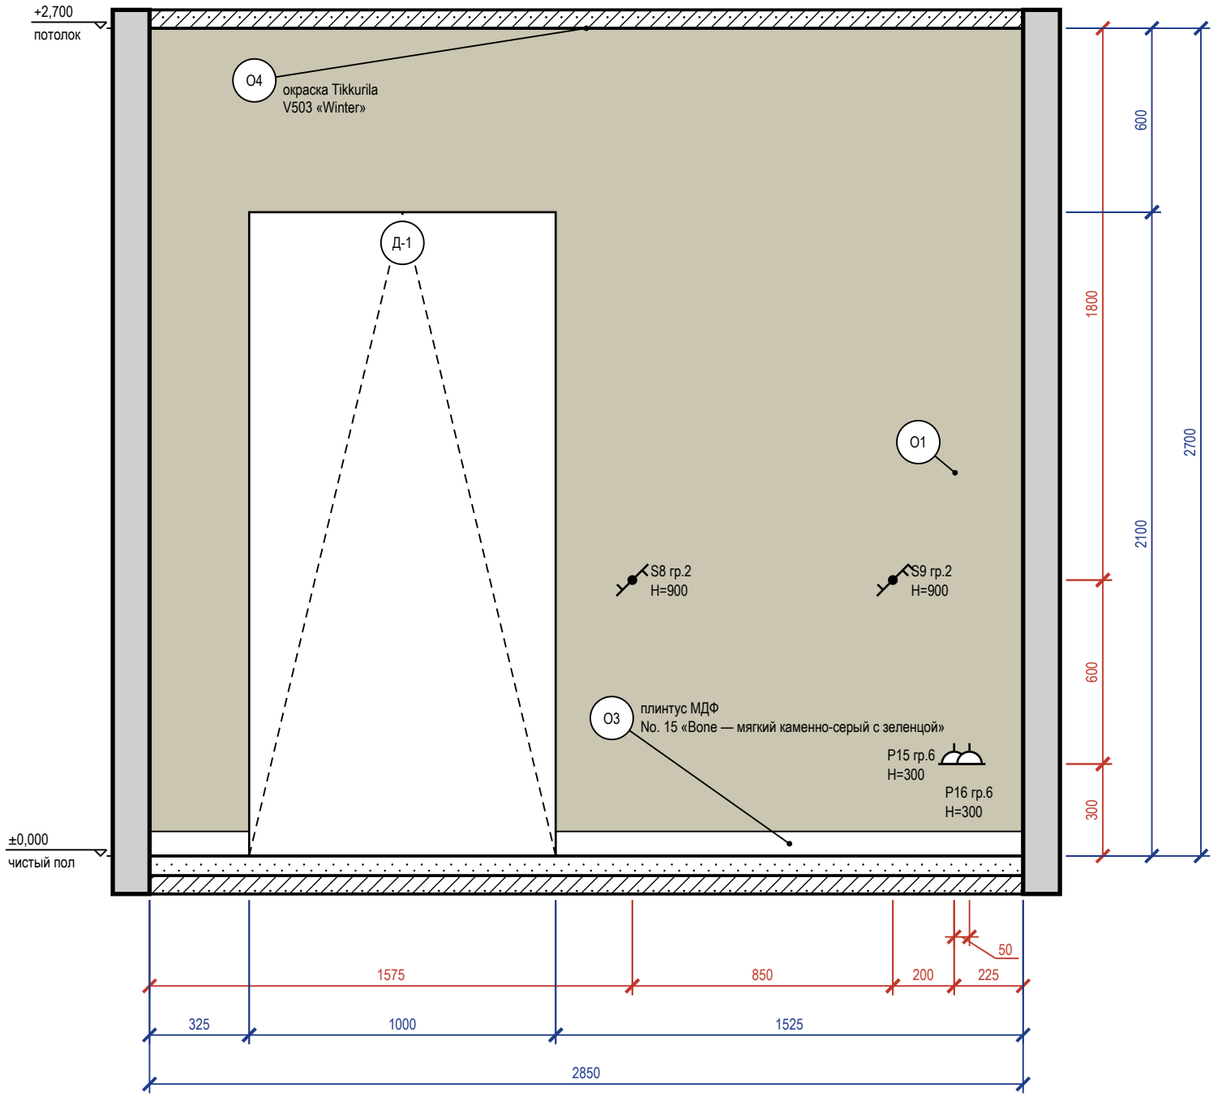


Схема развёрток (М 1:100)

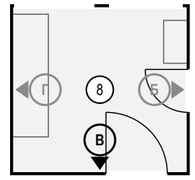

Ведомость отделки (на листе)

Марка	Поверхность	Материал, изделие	Цвет, код	Кол.
О1	стены	окраска, Farrow & Ball Modern Emulsion, матовая, подготовка Q3	Farrow & Ball No. 15 «Bone — мягкий каменно-серый с зеленцой»	5,6 м²
О3	плинтус	плинтус МДФ, h 80 мм, аналог: плинтус МДФ под покраску 80×16	Farrow & Ball No. 15 «Bone — мягкий каменно-серый с зеленцой»	1,9 м
О4	потолок	окраска, Tikkurila Anti-Reflex 2, глубокоматовая, подготовка Q3	Tikkurila V503 «Winter»	7,9 м²

Визуализация этой стены — лист 78



Примечания

1. Размеры — в мм от чистовых поверхностей стен; условные обозначения и общие указания — лист 2.

					Проект: Квартира с кабинетом
	Лист	№ док.	Подпись	Дата	Развёртка стены В. Прихожая (пом. 8)
Дизайнер	Кырлан А.С.			21.10.26	

Стадия	Лист	Листов
П	81	97

выпуск 18.10.2026 № 918b20bf25 · стр. 81 из 97

Правка к этому листу

Развёртка стены Г


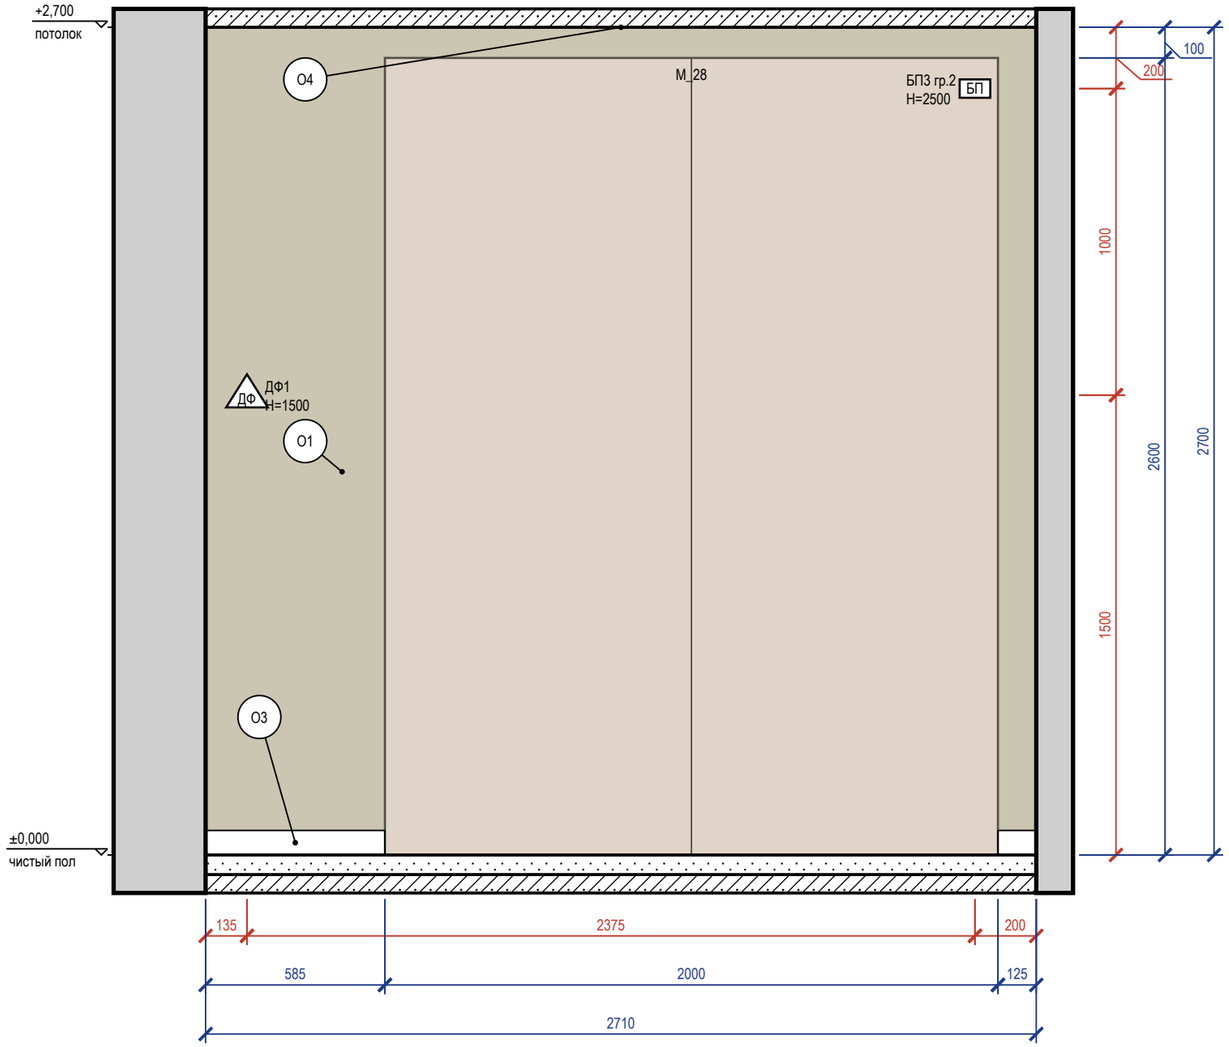


Схема развёрток (М 1:100)

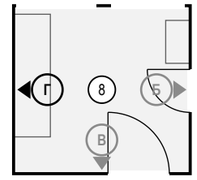

Ведомость отделки (на листе)

Марка	Поверхность	Материал, изделие	Цвет, код	Кол.
О1	стены	окраска, Farrow & Ball Modern Emulsion, матовая, подготовка Q3	Farrow & Ball No. 15 «Bone — мягкий каменно-серый с зеленцой»	7,3 м²
О3	плинтус	плинтус МДФ, h 80 мм, аналог: плинтус МДФ под покраску 80×16	Farrow & Ball No. 15 «Bone — мягкий каменно-серый с зеленцой»	0,7 м
О4	потолок	окраска, Tikkurila Anti-Reflex 2, глубокоматовая, подготовка Q3	Tikkurila V503 «Winter»	7,9 м²

Визуализация этой стены — лист 79



Примечания

1. Размеры — в мм от чистовых поверхностей стен; условные обозначения и общие указания — лист 2.

					Проект: Квартира с кабинетом
	Лист	№ док.	Подпись	Дата	Развёртка стены Г. Прихожая (пом. 8)
Дизайнер	Кырлан А.С.			21.10.26	

Стадия	Лист	Листов
П	82	97

выпуск 18.10.2026 № 918b20bf25 · стр. 82 из 97

Правка к этому листу



					Проект: Квартира с кабинетом	
	Лист	№ док.	Подпись	Дата		
Дизайнер	Кырлан А.С.			21.10.26	Визуализация: Санузел гостевой	Стадия: П; Лист: 83; Листов: 97

выпуск 18.10.2026 № 918b20bf25 · стр. 83 из 97

Правка к этому листу



					Проект: Квартира с кабинетом
	Лист	№ док.	Подпись	Дата	
Дизайнер	Кырлан А.С.			21.10.26	Визуализация: Санузел гостевой

Стадия	Лист	Листов
П	84	97

выпуск 18.10.2026 № 918b20bf25 · стр. 84 из 97

Правка к этому листу

Развёртка стены А


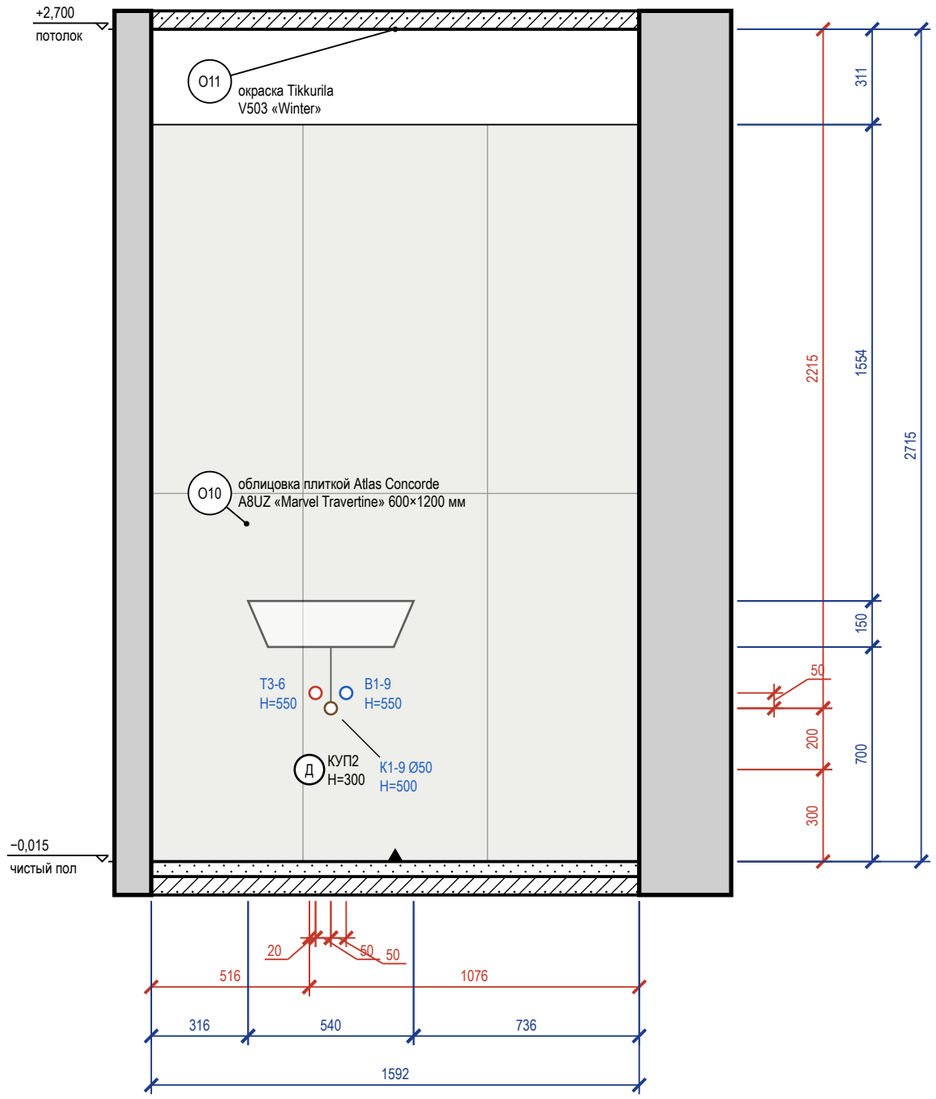


Схема развёрток (М 1:100)

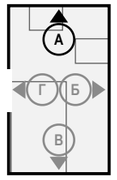

Ведомость отделки (на листе)

Марка	Поверхность	Материал, изделие	Цвет, код	Кол.
О10	стены	облицовка плиткой, Atlas Concorde Marvel Travertine, 600×1200×9 мм, A8UZ, затирка CG2WA	Atlas Concorde A8UZ «Marvel Travertine»	3,8 м²
О11	потолок	окраска, Tikkurila Luja 7, матовая, подготовка Q3	Tikkurila V503 «Winter»	4,5 м²

Визуализация этой стены — лист 84



Примечания

1. Размеры — в мм от чистовых поверхностей стен; условные обозначения и общие указания — лист 2.
2. Облицовка — по сетке швов 2 мм, раскладка от оси стены (треугольник у пола), целые ряды от пола; подрезки — по листу раскладки плитки.
3. Гидроизоляция в 2 слоя, заход на стены 200 мм — до облицовки, с актом скрытых работ и тестом проливом (узел — на листе узлов).


					Проект: Квартира с кабинетом
	Лист	№ док.	Подпись	Дата	Развёртка стены А. Санузел гостевой (пом. 9)
Дизайнер	Кырлан А.С.			21.10.26	

Стадия	Лист	Листов
П	85	97

выпуск 18.10.2026 № 918b20bf25 · стр. 85 из 97

Правка к этому листу

Развёртка стены Б

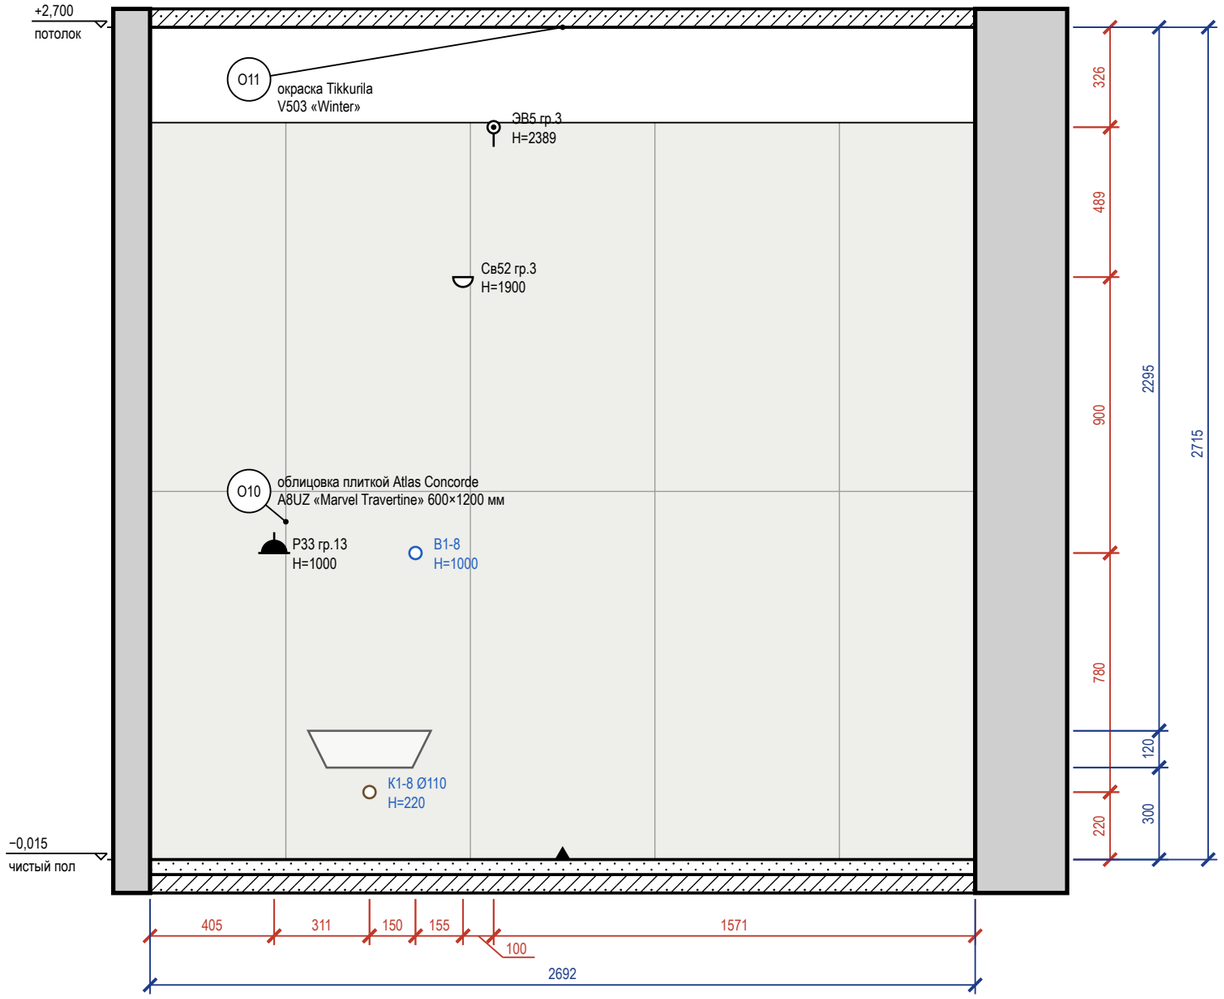

Развёртка стены В


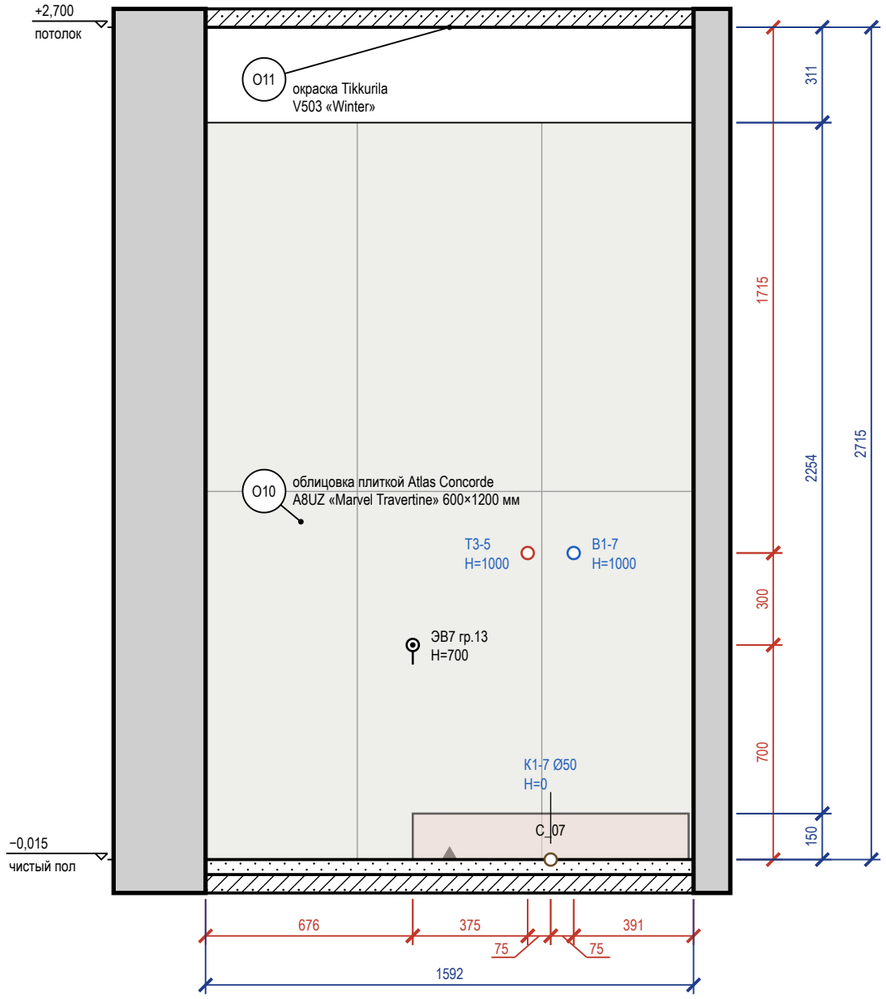


Схема развёрток (М 1:100)

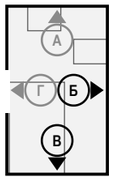

Ведомость отделки (на листе)

Марка	Поверхность	Материал, изделие	Цвет, код	Кол.
О10	стены	облицовка плиткой, Atlas Concorde Marvel Travertine, 600×1200×9 мм, A8UZ, затирка CG2WA	Atlas Concorde A8UZ «Marvel Travertine»	10,3 м²
О11	потолок	окраска, Tikkurila Luja 7, матовая, подготовка Q3	Tikkurila V503 «Winter»	4,5 м²

Визуализация этой стены — лист 83



Примечания

1. Размеры — в мм от чистовых поверхностей стен; условные обозначения и общие указания — лист 2.
2. Схема мебели, приборов и декора не является технической документацией для производства мебели; габариты — по паспортам изделий.
3. Облицовка — по сетке швов 2 мм, раскладка от оси стены (треугольник у пола), целые ряды от пола; подрезки — по листу раскладки плитки.
4. Гидроизоляция в 2 слоя, заход на стены 200 мм — до облицовки, с актом скрытых работ и тестом проливом (узел — на листе узлов).

					Проект: Квартира с кабинетом
	Лист	№ док.	Подпись	Дата	Развёртки стен Б, В. Санузел гостевой (пом. 9)
Дизайнер	Кырлан А.С.			21.10.26	

Стадия	Лист	Листов
П	86	97

выпуск 18.10.2026 № 918b20bf25 · стр. 86 из 97

Правка к этому листу

Развёртка стены Г


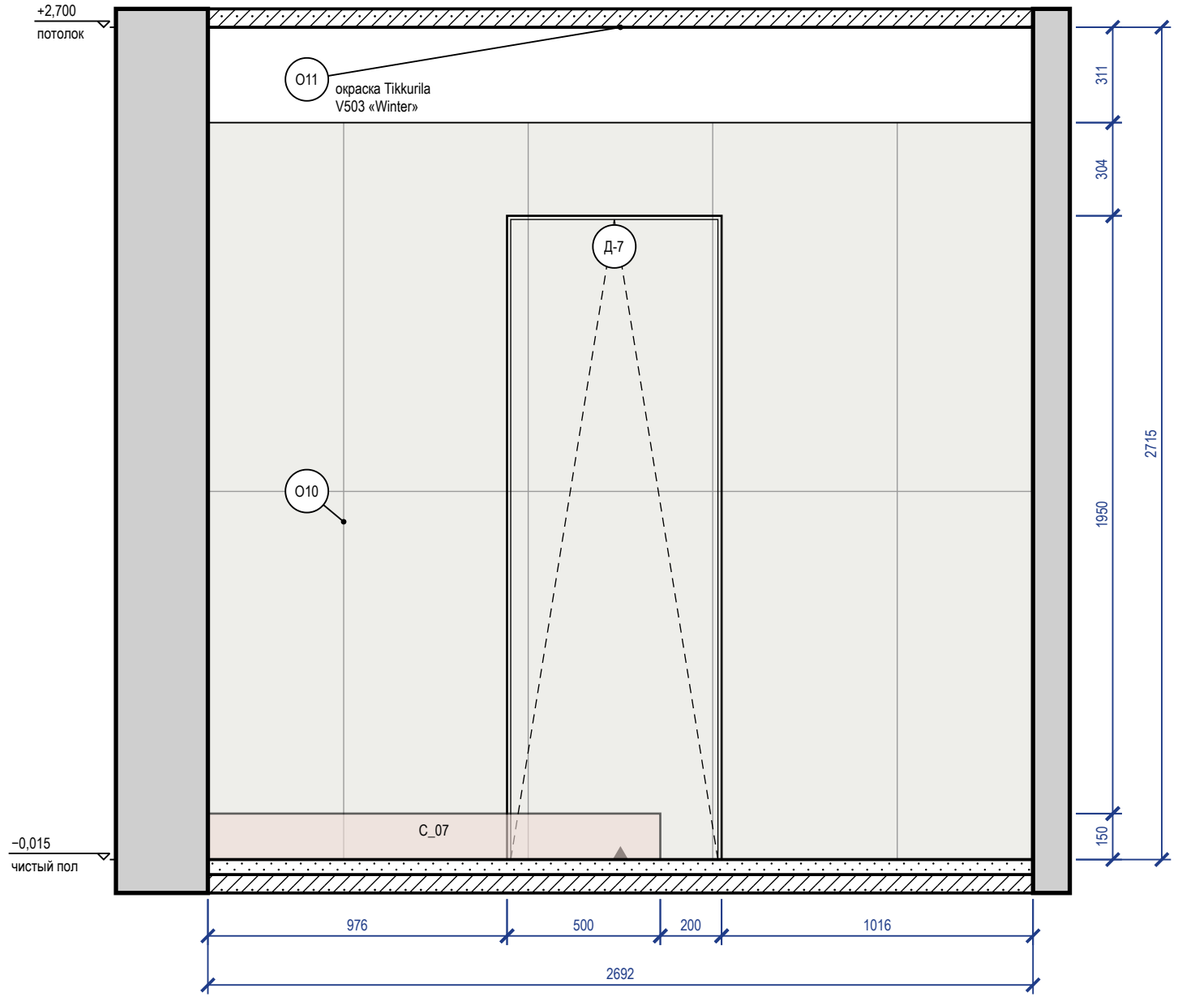


Схема развёрток (М 1:100)

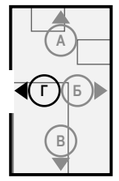

Ведомость отделки (на листе)

Марка	Поверхность	Материал, изделие	Цвет, код	Кол.
О10	стены	облицовка плиткой, Atlas Concorde Marvel Travertine, 600×1200×9 мм, A8UZ, затирка CG2WA	Atlas Concorde A8UZ «Marvel Travertine»	5 м²
О11	потолок	окраска, Tikkurila Luja 7, матовая, подготовка Q3	Tikkurila V503 «Winter»	4,5 м²

Примечания


1. Размеры — в мм от чистовых поверхностей стен; условные обозначения и общие указания — лист 2.
2. Схема мебели, приборов и декора не является технической документацией для производства мебели; габариты — по паспортам изделий.
3. Облицовка — по сетке швов 2 мм, раскладка от оси стены (треугольник у пола), целые ряды от пола; подрезки — по листу раскладки плитки.
4. Гидроизоляция в 2 слоя, заход на стены 200 мм — до облицовки, с актом скрытых работ и тестом проливом (узел — на листе узлов).
5. Двери скрытого монтажа — полотно в плоскости стены, отделка стены по полотну, плинтус прерывается у короба (узел — на листе узлов).

					Проект: Квартира с кабинетом	
	Лист	№ док.	Подпись	Дата	Развёртка стены Г. Санузел гостевой (пом. 9)	Стадия / Лист / Листов
Дизайнер	Кырлан А.С.			21.10.26		П / 87 / 97


выпуск 18.10.2026 № 918b20bf25 · стр. 87 из 97

Правка к этому листу


Общий вид

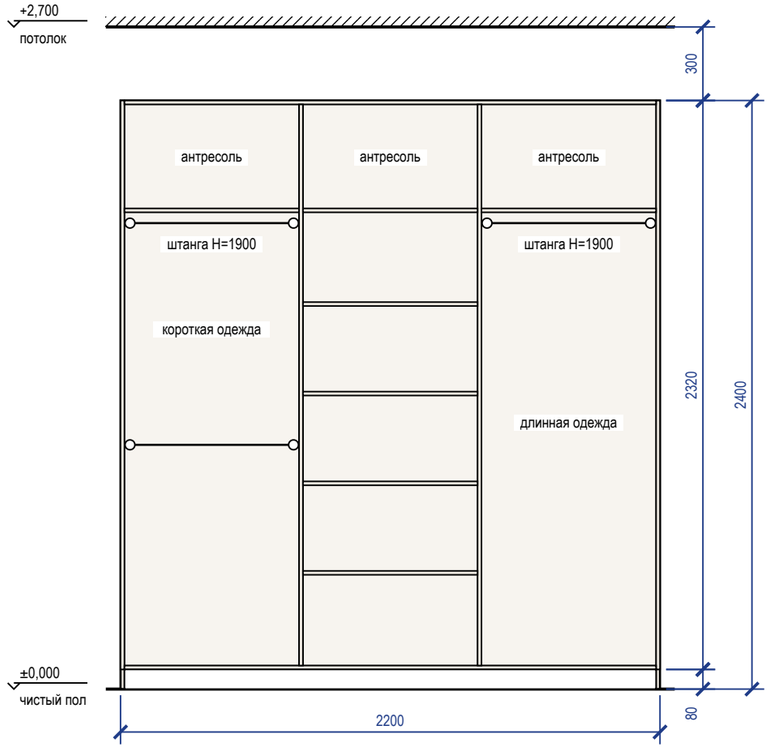


Наполнение, размеры в свету

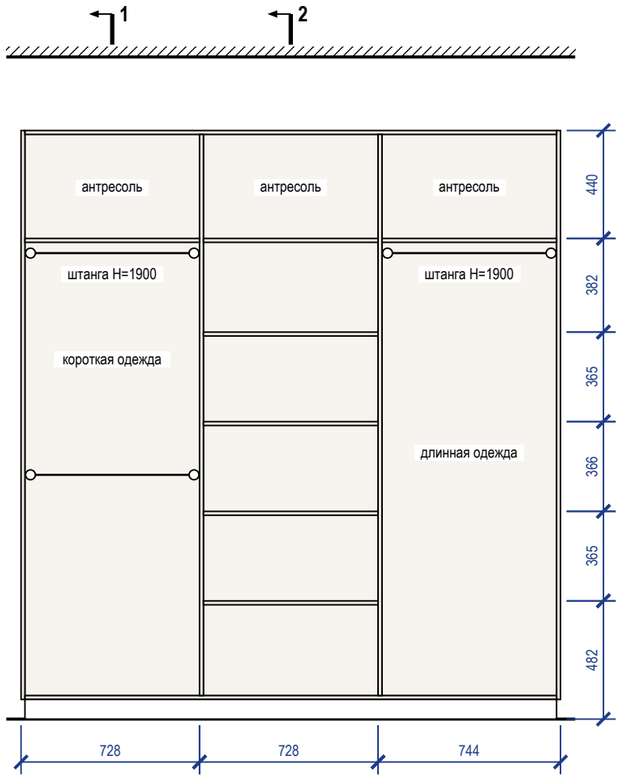

Разрез 1-1

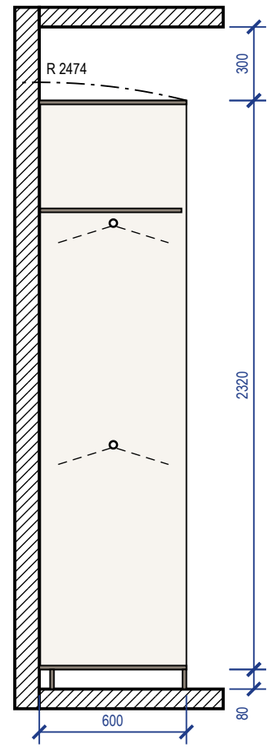


Разрез 2-2

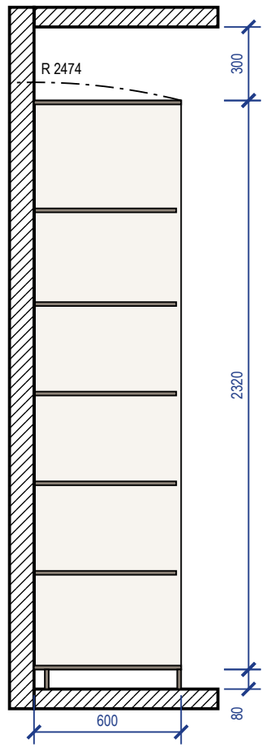

Примечания

1. Размеры — в мм по чистовой отделке; изделие 2200×600×2400 (Ш×Г×В). Перед раскроем — контрольный замер цеха после чистовой отделки стен, пола и потолка.
2. Корпус — ЛДСП 16 мм, задняя стенка ХДФ 4 мм в паз, цоколь 80 мм на регулируемых опорах; открытая система без фасадов, ящики с фасадами.
3. Кромка: скрытые торцы 0,4 мм, видимые 2 мм (ПВХ/АБС).
4. Номинальные зазоры: между фасадами ящиков 3 мм, фасад ящика — стойка 2 мм.
5. Ящики — направляющие полного выдвижения NL 550 (внутренняя глубина 596 мм ≥ NL + 3); присадка по 32-й системе — выполняет цех.
6. Зазор до потолка 300 мм.
7. Подъём корпуса: диагональ боковины $\sqrt{(2400^2 + 600^2)} = 2474$ мм < 2700 мм до потолка — корпус собирается лёжа и поднимается поворотом.
8. Крепление к стене от опрокидывания: крепление к стене, 3 точки; основание стены и шаг анкеров — монтажная схема шкафов.

3D орто

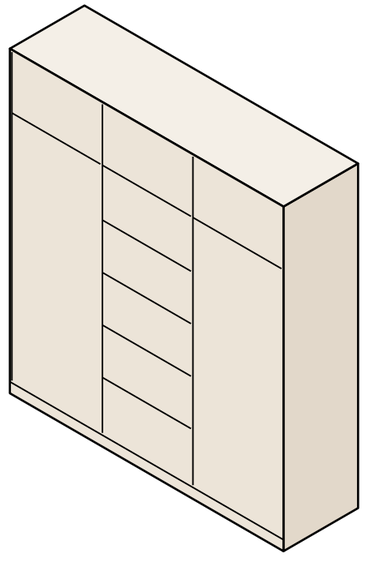


					Проект: Квартира с кабинетом
	Лист	№ док.	Подпись	Дата	
Дизайнер	Кырлан А.С.			21.10.26	Система хранения M_06

Стадия	Лист	Листов
П	Д_1	97


выпуск 18.10.2026 № 918b20bf25 · стр. 88 из 97

Правка к этому листу


Общий вид

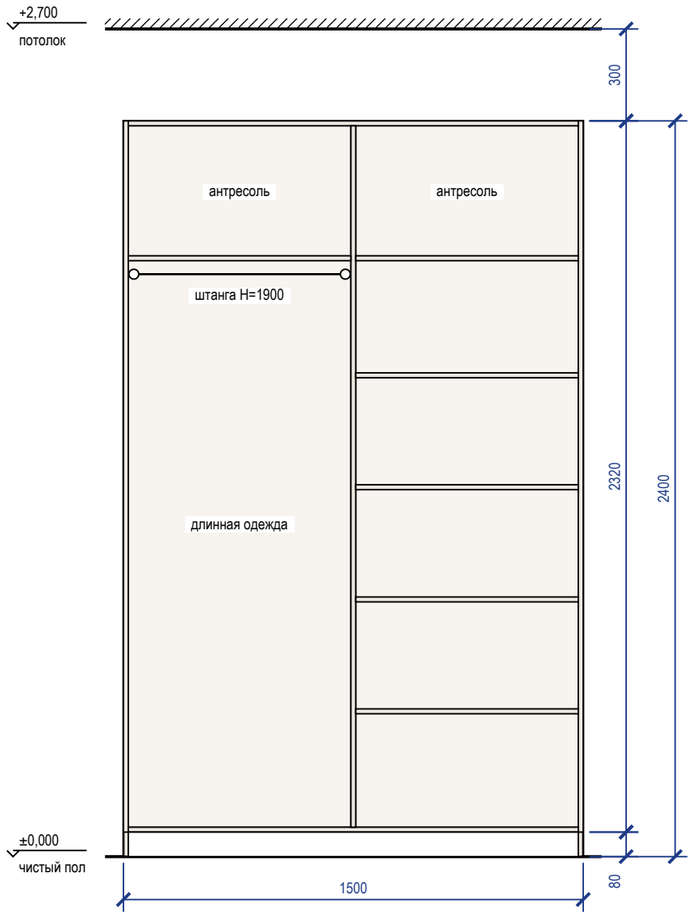


Наполнение, размеры в свету

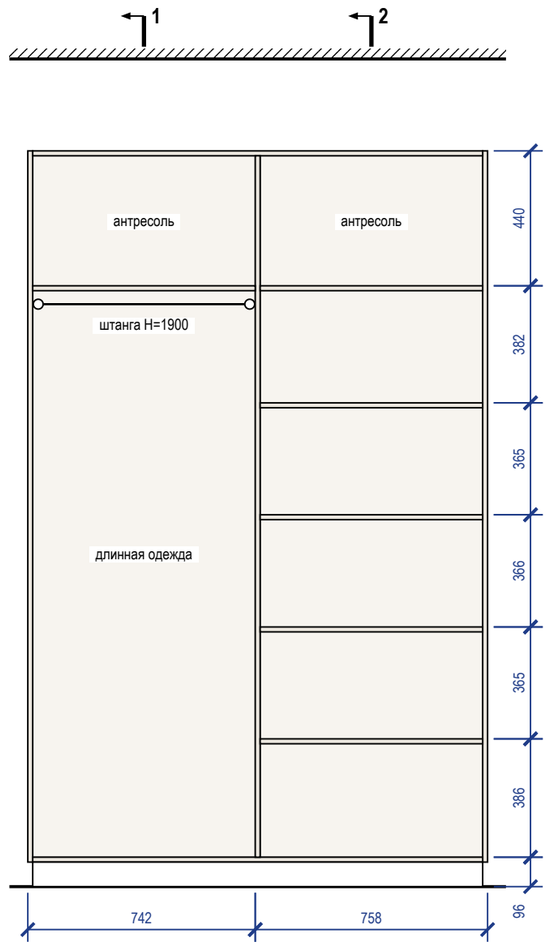

Разрез 1-1

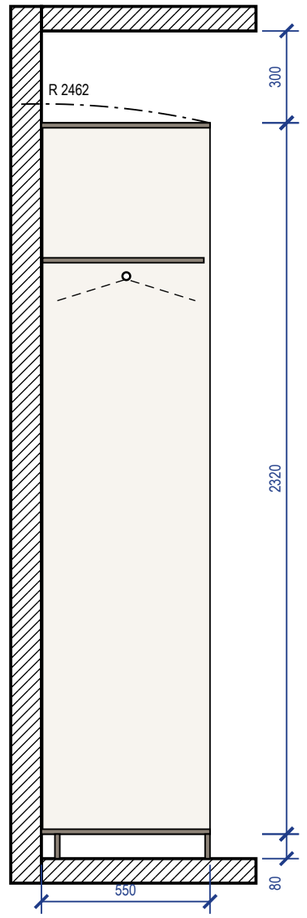


Разрез 2-2

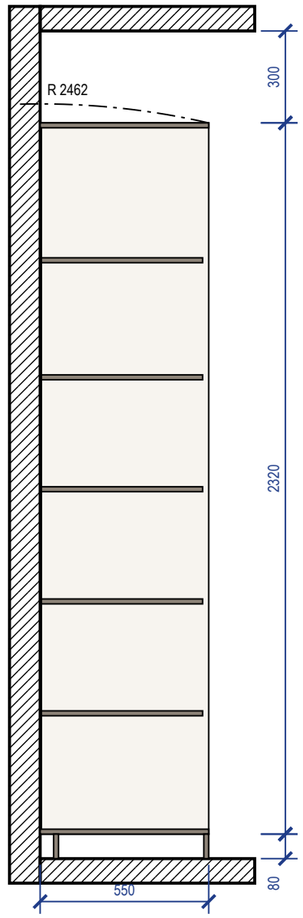

Примечания

1. Размеры — в мм по чистовой отделке; изделие 1500×550×2400 (Ш×Г×В). Перед раскроем — контрольный замер цеха после чистовой отделки стен, пола и потолка.
2. Корпус — ЛДСП 16 мм, задняя стенка ХДФ 4 мм в паз, цоколь 80 мм на регулируемых опорах; открытая система без фасадов, ящики с фасадами.
3. Кромка: скрытые торцы 0,4 мм, видимые 2 мм (ПВХ/АБС).
4. Номинальные зазоры: между фасадами ящиков 3 мм, фасад ящика — стойка 2 мм.
5. Ящики — направляющие полного выдвижения NL 500 (внутренняя глубина 546 мм ≥ NL + 3); присадка по 32-й системе — выполняет цех.
6. Зазор до потолка 300 мм.
7. Подъём корпуса: диагональ боковины $\sqrt{(2400^2 + 550^2)} = 2462$ мм < 2700 мм до потолка — корпус собирается лёжа и поднимается поворотом.
8. Крепление к стене от опрокидывания: крепление к стене, 3 точки; основание стены и шаг анкеров — монтажная схема шкафов.

3D орто

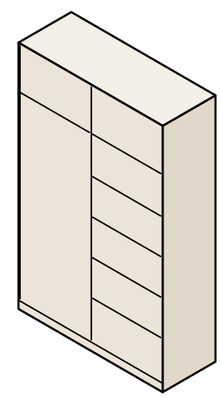


					Проект: Квартира с кабинетом
	Лист	№ док.	Подпись	Дата	Система хранения M_07
Дизайнер	Кырлан А.С.			21.10.26	

Стадия	Лист	Листов
П	Д_2	97


выпуск 18.10.2026 № 918b20bf25 · стр. 89 из 97

Правка к этому листу


Вид с фасадами

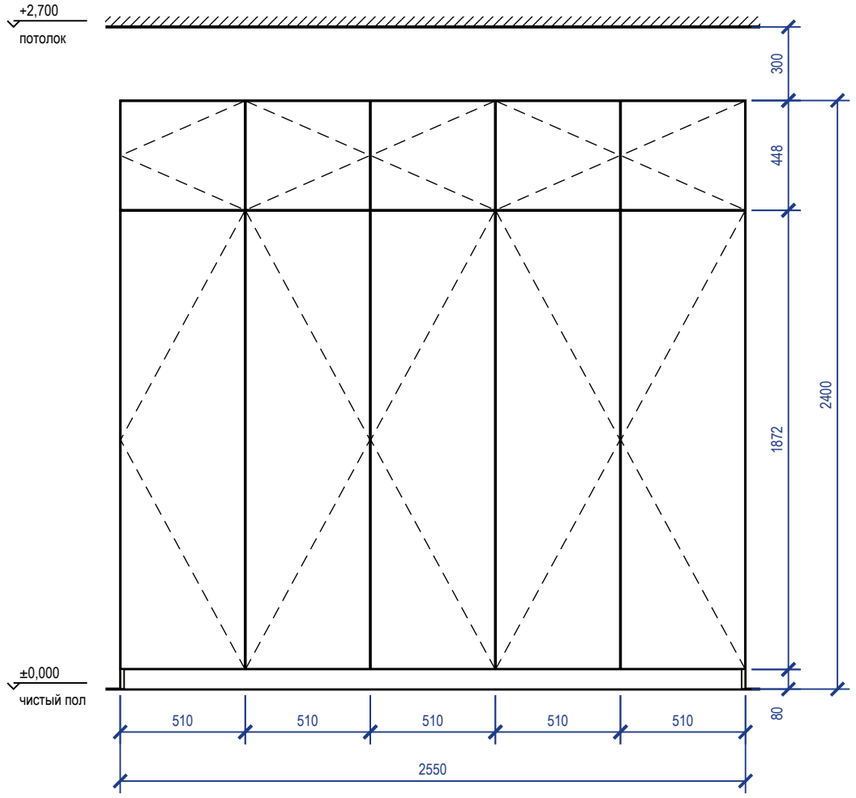


Вид без фасадов

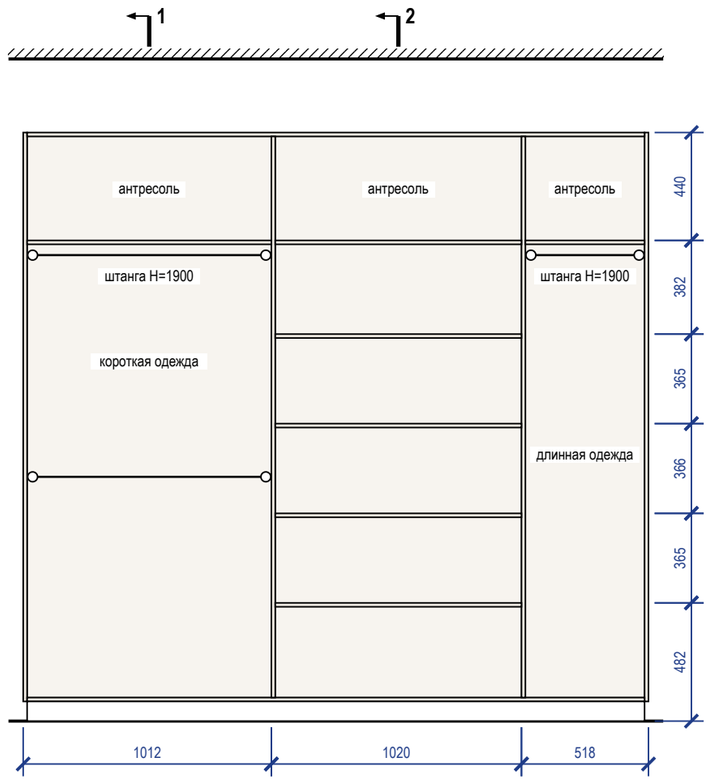

Разрез 1-1

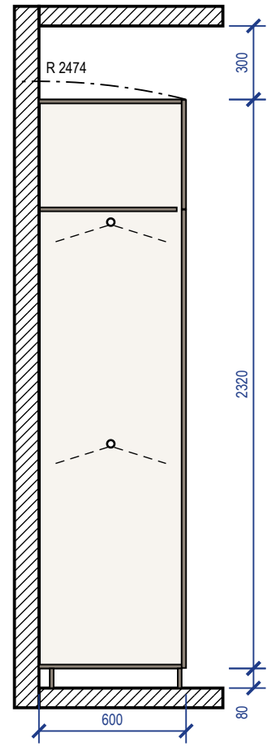


Разрез 2-2

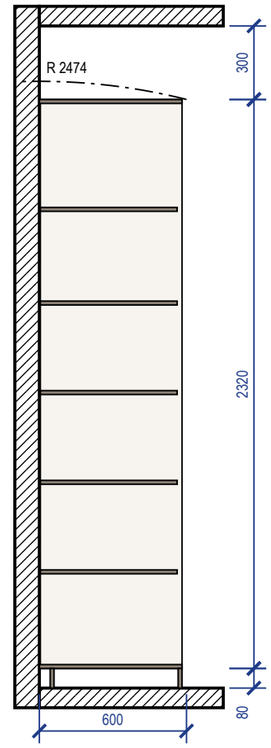

Примечания

1. Размеры — в мм по чистовой отделке; изделие 2550×600×2400 (Ш×Г×В). Перед раскроем — контрольный замер цеха после чистовой отделки стен, пола и потолка.
2. Корпус — ЛДСП 16 мм, задняя стенка ХДФ 4 мм в паз, цоколь 80 мм на регулируемых опорах; фасады — МДФ, эмаль матовая 18 мм накладные, цвет — по колерной карте; петли с доводчиком: фасад 1869 мм — 4 петли, фасад 445 мм — 2 петли.
3. Кромка: скрытые торцы 0,4 мм, видимые 2 мм (ПВХ/АБС).
4. Номинальные зазоры: между фасадами 3 мм, фасад — стена и фасад — потолок не менее 3 мм, фасад ящика — стойка 2 мм.
5. Ящики — направляющие полного выдвижения NL 550 (внутренняя глубина 578 мм ≥ NL + 3); присадка по 32-й системе — выполняет цех.
6. Зазор до потолка 300 мм.
7. Подъём корпуса: диагональ боковины $\sqrt{(2400^2 + 600^2)} = 2474$ мм < 2700 мм до потолка — корпус собирается лёжа и поднимается поворотом.
8. Крепление к стене от опрокидывания — уголки 2 шт. к несущему основанию (монтажная схема шкафов).

3D орто

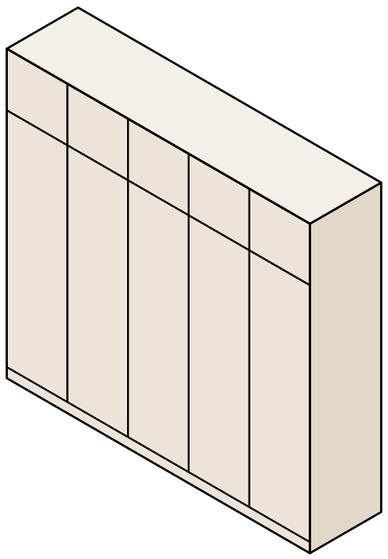


					Проект: Квартира с кабинетом
	Лист	№ док.	Подпись	Дата	
Дизайнер	Кырлан А.С.			21.10.26	Шкаф распашной M_08

Стадия	Лист	Листов
П	Д_3	97


выпуск 18.10.2026 № 918b20bf25 · стр. 90 из 97

Правка к этому листу


Вид с фасадами

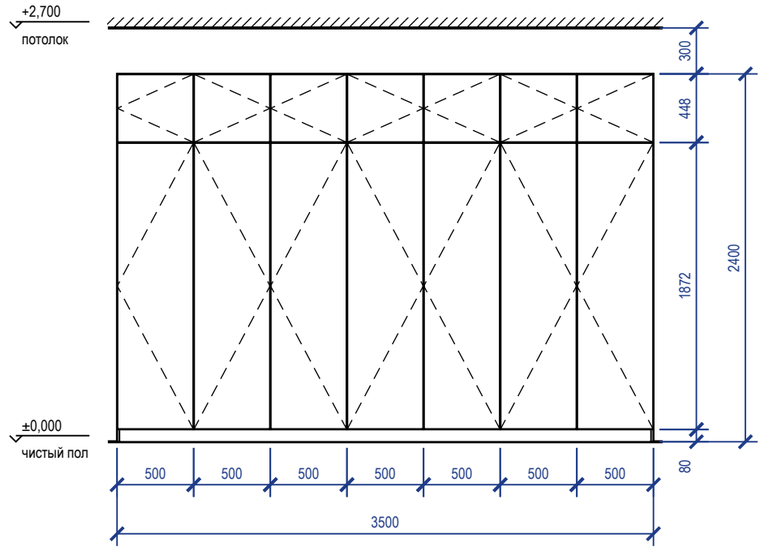


Вид без фасадов

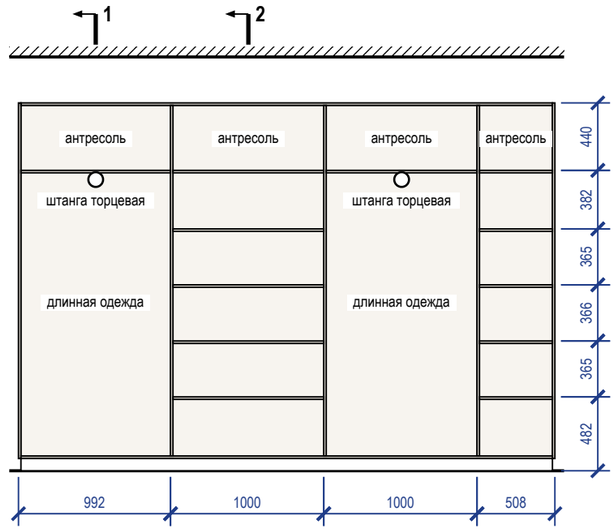

Разрез 1-1

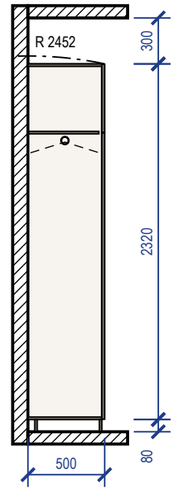


Разрез 2-2

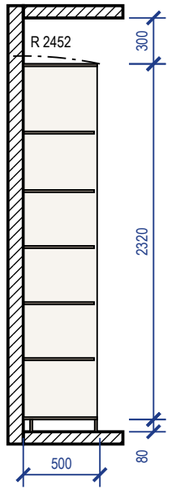

Примечания

1. Размеры — в мм по чистовой отделке; изделие 3500×500×2400 (Ш×Г×В). Перед раскроем — контрольный замер цеха после чистовой отделки стен, пола и потолка.
2. Корпус — ЛДСП 16 мм, задняя стенка ХДФ 4 мм в паз, цоколь 80 мм на регулируемых опорах; фасады — МДФ, эмаль матовая 18 мм накладные, цвет — по колерной карте; петли с доводчиком: фасад 1869 мм — 4 петли, фасад 445 мм — 2 петли.
3. Кромка: скрытые торцы 0,4 мм, видимые 2 мм (ПВХ/АБС).
4. Номинальные зазоры: между фасадами 3 мм, фасад — стена и фасад — потолок не менее 3 мм, фасад ящика — стойка 2 мм.
5. Ящики — направляющие полного выдвижения NL 450 (внутренняя глубина 478 мм ≥ NL + 3); присадка по 32-й системе — выполняет цех.
6. Зазор до потолка 300 мм.
7. Подъём корпуса: диагональ боковины $\sqrt{(2400^2 + 500^2)} = 2452$ мм < 2700 мм до потолка — корпус собирается лёжа и поднимается поворотом.
8. Крепление к стене от опрокидывания — уголки 2 шт. к несущему основанию (монтажная схема шкафов).

3D орто

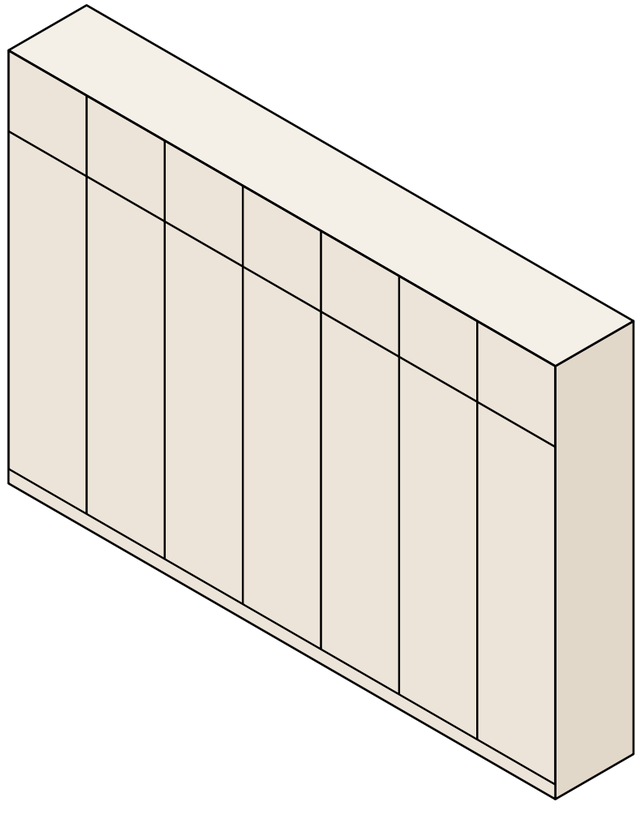


					Проект: Квартира с кабинетом
	Лист	№ док.	Подпись	Дата	Шкаф распашной М_24
Дизайнер	Кырлан А.С.			21.10.26	

Стадия	Лист	Листов
П	Д_4	97


выпуск 18.10.2026 № 918b20bf25 · стр. 91 из 97

Правка к этому листу


Вид с фасадами

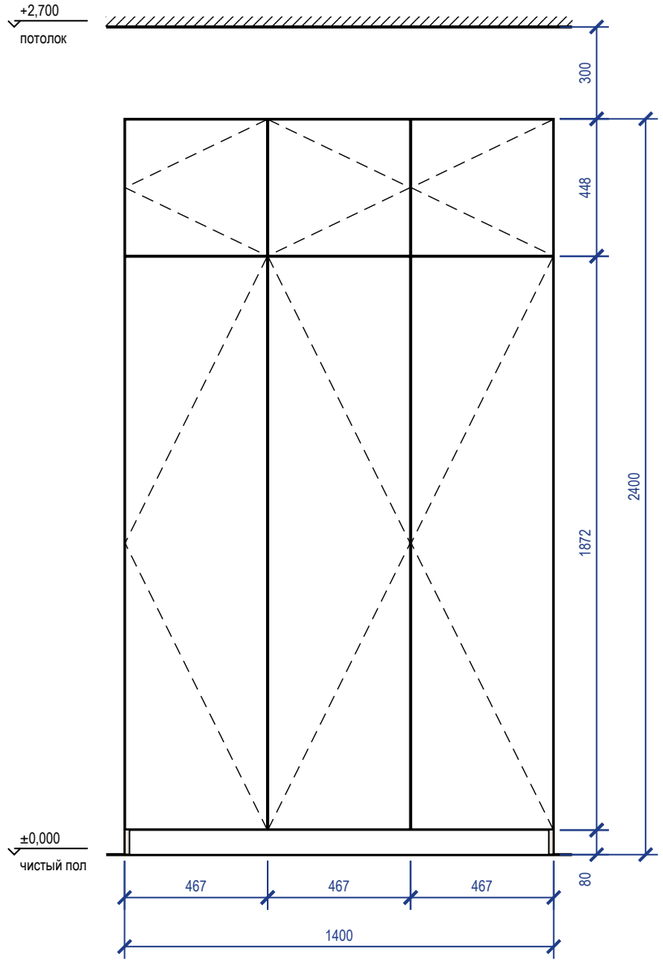


Вид без фасадов

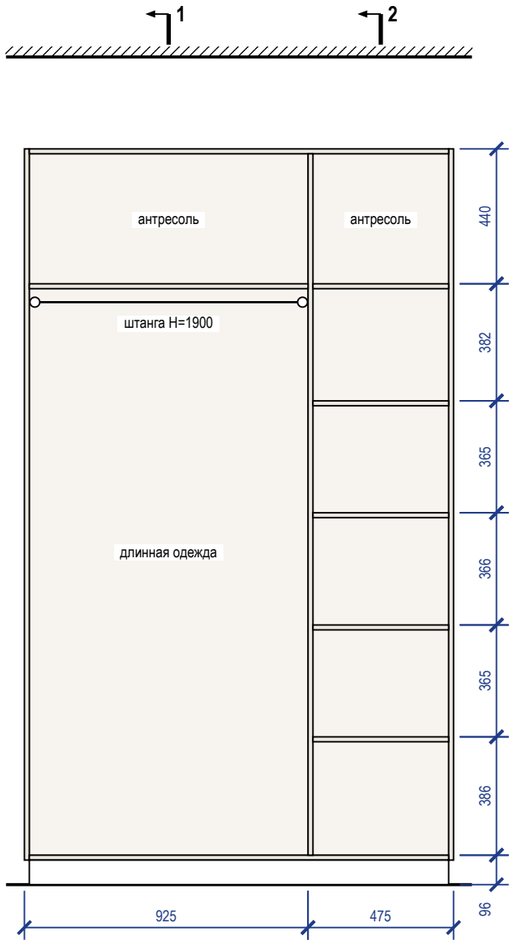

Разрез 1-1

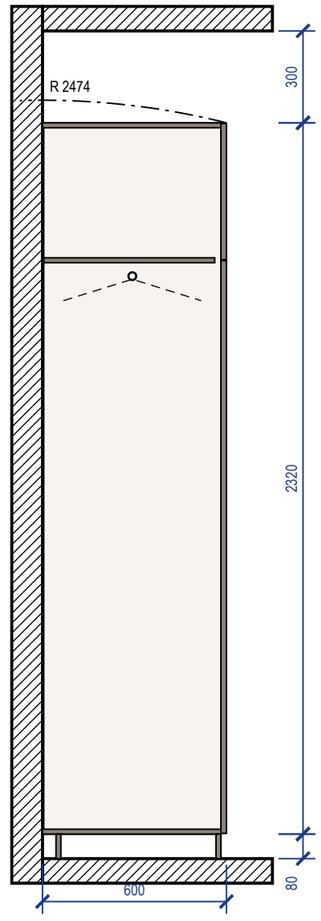


Разрез 2-2

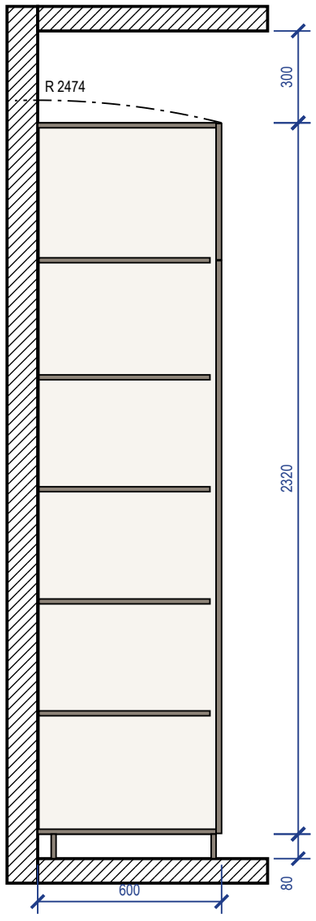

Примечания

1. Размеры — в мм по чистовой отделке; изделие 1400×600×2400 (Ш×Г×В). Перед раскроем — контрольный замер цеха после чистовой отделки стен, пола и потолка.
2. Корпус — ЛДСП 16 мм, задняя стенка ХДФ 4 мм в паз, цоколь 80 мм на регулируемых опорах; фасады — МДФ, эмаль матовая 18 мм накладные, цвет — по колерной карте; петли с доводчиком: фасад 1869 мм — 4 петли, фасад 445 мм — 2 петли.
3. Кромка: скрытые торцы 0,4 мм, видимые 2 мм (ПВХ/АБС).
4. Номинальные зазоры: между фасадами 3 мм, фасад — стена и фасад — потолок не менее 3 мм, фасад ящика — стойка 2 мм.
5. Ящики — направляющие полного выдвижения NL 550 (внутренняя глубина 578 мм ≥ NL + 3); присадка по 32-й системе — выполняет цех.
6. Зазор до потолка 300 мм.
7. Подъём корпуса: диагональ боковины $\sqrt{(2400^2 + 600^2)} = 2474$ мм < 2700 мм до потолка — корпус собирается лёжа и поднимается поворотом.
8. Крепление к стене от опрокидывания: крепление к стене, 2 точки; основание стены и шаг анкеров — монтажная схема шкафов.

3D орто

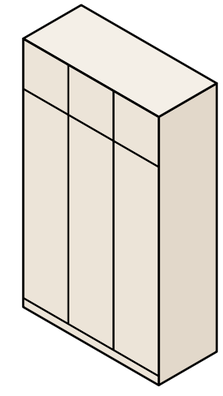


					Проект: Квартира с кабинетом
	Лист	№ док.	Подпись	Дата	
Дизайнер	Кырлан А.С.			21.10.26	Шкаф распашной М_25
					Стадия: П; Лист: Д_5; Листов: 97


выпуск 18.10.2026 № 918b20bf25 · стр. 92 из 97

Правка к этому листу


Вид с фасадами

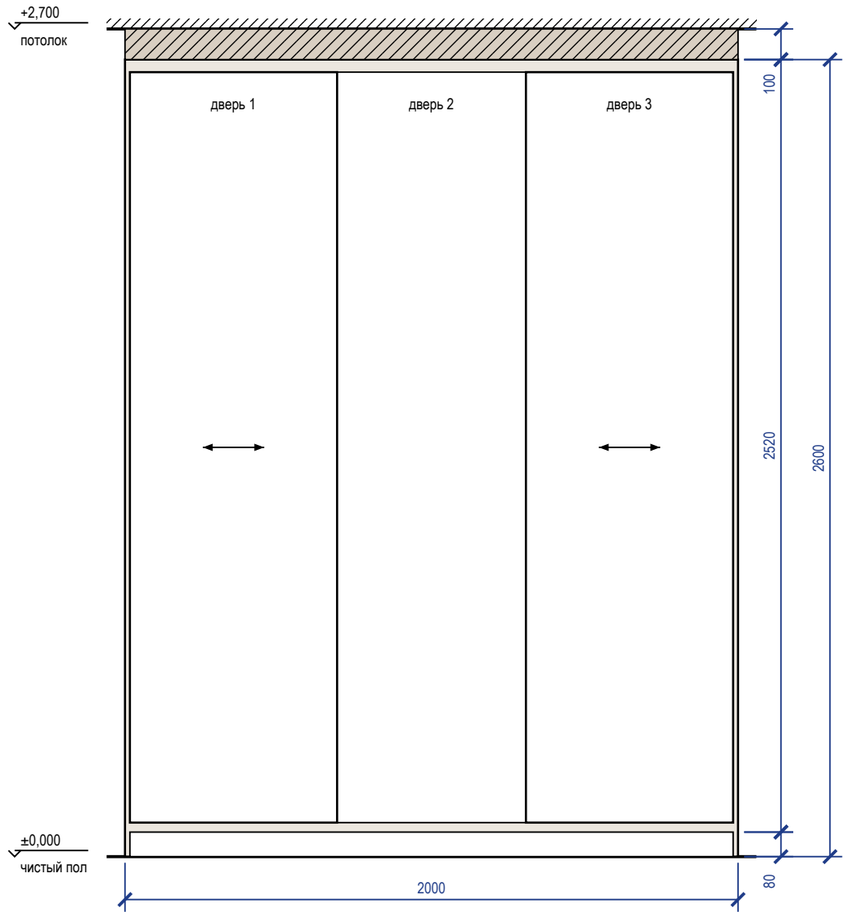


Вид без фасадов

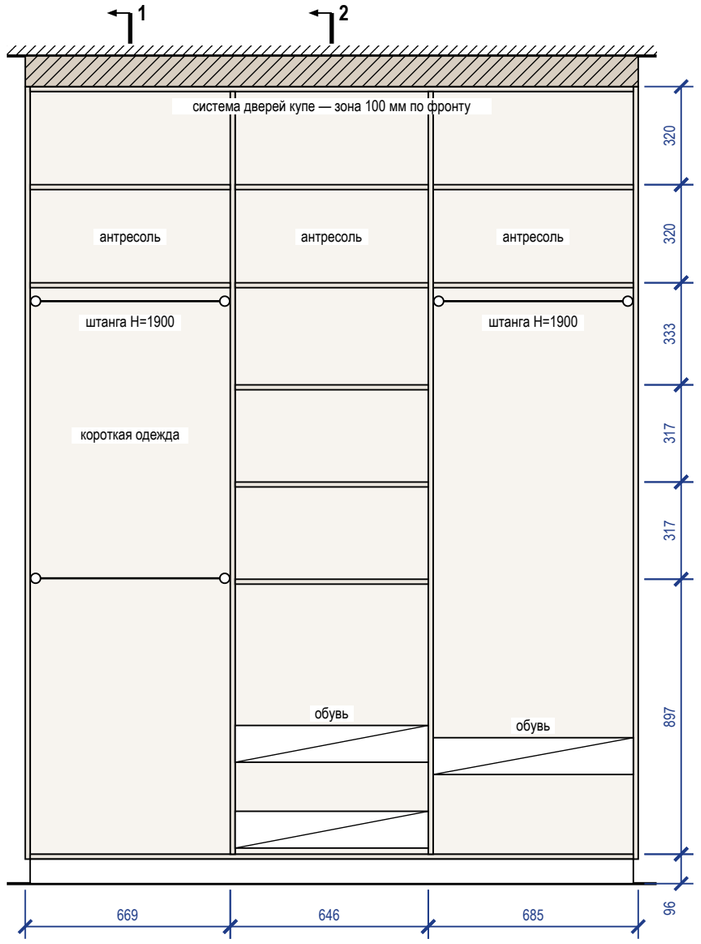

Разрез 1-1

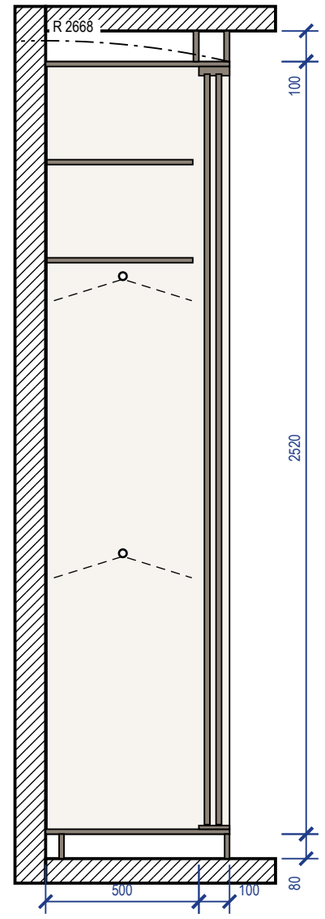


Разрез 2-2

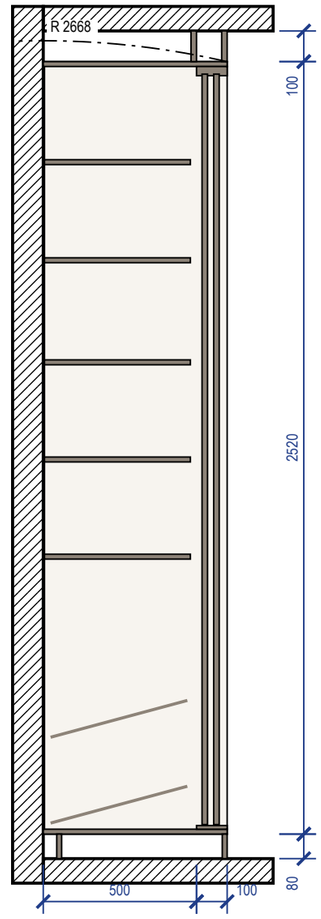

Примечания

1. Размеры — в мм по чистовой отделке; изделие 2000×600×2600 (Ш×Г×В). Перед раскроем — контрольный замер цеха после чистовой отделки стен, пола и потолка.
2. Корпус — ЛДСП 16 мм, задняя стенка ХДФ 4 мм в паз, цоколь 80 мм на регулируемых опорах; двери купе — ЛДСП 10 мм в алюминиевом профиле, нахлёст 30 мм, ширина двери 676 мм, высота — проём минус 40 мм; цвет — по колерной карте.
3. Кромка: скрытые торцы 0,4 мм, видимые 2 мм (ПВХ/АБС).
4. Номинальные зазоры: дверь купе — боковина 3 мм, фасад ящика — стойка 2 мм; ящики внутри купе — с накладкой 30 мм на стойке со стороны нахлёста дверей.
5. Ящики — направляющие полного выдвижения NL 450 (внутренняя глубина 496 мм ≥ NL + 3); присадка по 32-й системе — выполняет цех.
6. Компенсатор 100 мм — короб из ЛДСП по фронту и торцам, подгоняется к потолку при монтаже (припуск 20 мм), крепится к корпусу и к потолку.
7. Подъём корпуса: диагональ боковины $\sqrt{(2600^2 + 600^2)} = 2668$ мм < 2700 мм до потолка — корпус собирается лёжа и поднимается поворотом.
8. Крепление к стене от опрокидывания — уголки 2 шт. к несущему основанию (монтажная схема шкафов).

3D орто

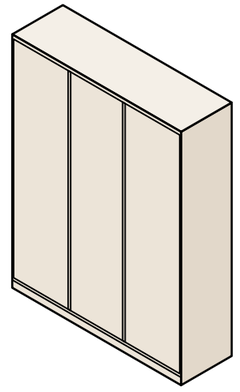


					Проект: Квартира с кабинетом
	Лист	№ док.	Подпись	Дата	
Дизайнер	Кырлан А.С.			21.10.26	Шкаф-купе M_28

Стадия	Лист	Листов
П	Д_6	97


выпуск 18.10.2026 № 918b20bf25 · стр. 93 из 97

Правка к этому листу


Вид с фасадами

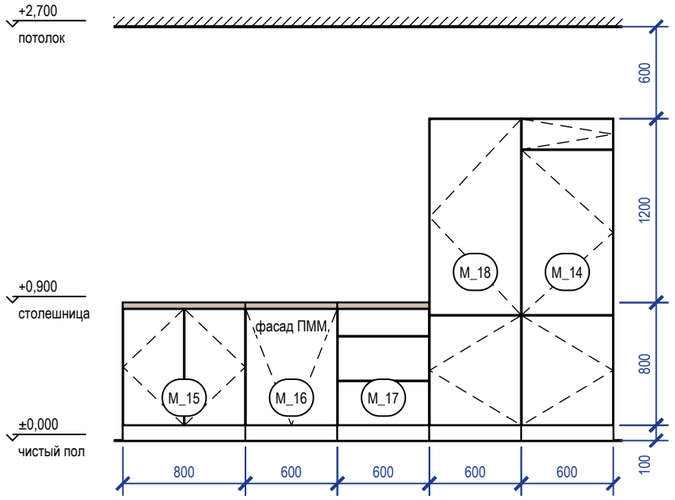


Вид без фасадов (наполнение, выводы)

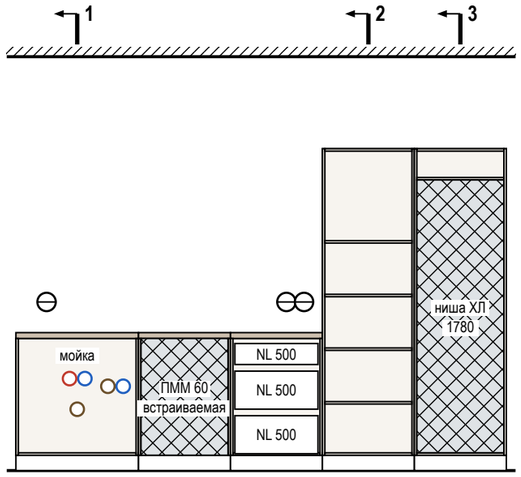


Разрез 1-1

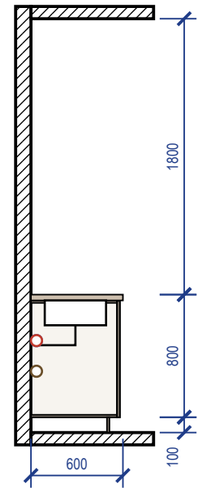


Разрез 2-2

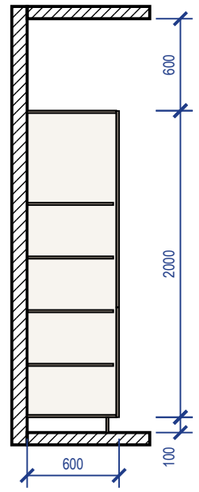

Разрез 3-3

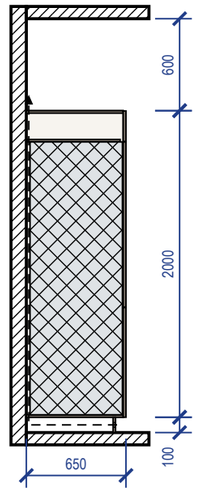

3D орто

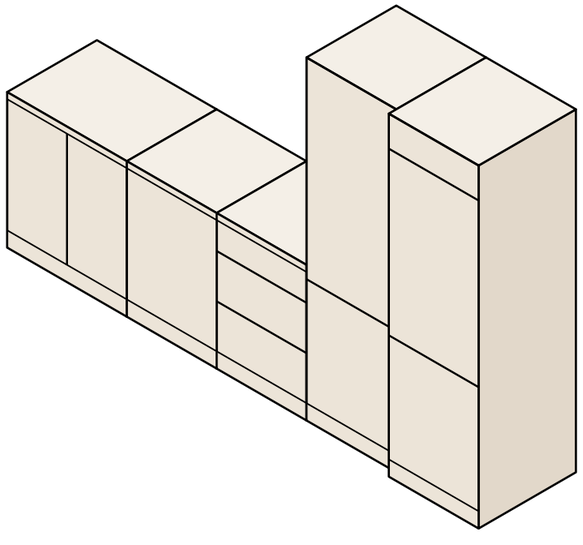

Примечания

1. Размеры — в мм по чистовой отделке, вид из помещения; марки — как на плане расстановки. Перед раскроем — контрольный замер цеха после фартука и пола.
2. Корпуса — ЛДСП 16 мм, задняя стенка ХДФ 4 мм; фасады — МДФ, эмаль матовая 18 мм, цвет по колерной карте; столешница 38 мм, свес 20 мм; цоколь 100 мм.
3. Кромка: скрытые торцы 0,4 мм, видимые 2 мм. Номинальные зазоры: между фасадами 3 мм, фасад — столешница 3 мм, фасад — стена не менее 3 мм.
4. Ящики полного выдвижения и петли — с доводчиком; присадка по 32-й системе — выполняет цех.
5. Ниши техники (холодильник — ориентир 1780 мм) — по монтажным схемам выбранных моделей: решётка в цоколе и канал за пеналом холодильника, зазор за духовым шкафом, фасад ПММ на двери машины.

					Проект: Квартира с кабинетом	
	Лист	№ док.	Подпись	Дата	Кухня (пом. 4). Развёртка гарнитура	Стадия / Лист / Листов
Дизайнер	Кырлан А.С.			21.10.26		П / Д_7 / 97

выпуск 18.10.2026 № 918b20bf25 · стр. 94 из 97

Правка к этому листу

Ведомость отделки помещений (форма 1 прил. А ГОСТ 21.501-2018)

№	Наименование помещения	Потолок			Стены и перегородки			Низ стен (плинтус)			Пол		Примечание
		Вид отделки	Код цвета	S, м²	Вид отделки	Код цвета	S, м²	Вид отделки	Код цвета	L, м	Вид отделки	S, м²	
1	Спальня 17,89 м²	Окраска, Tikkurila Anti-Reflex 2, глубокоматовая, 2 слоя, подготовка Q3	Tikkurila V503	17,89	Окраска, Farrow & Ball Modern Emulsion, матовая, 2 слоя, подготовка Q3 Акцент — стена А: окраска, Farrow & Ball Modern Emulsion, матовая, 2 слоя, подготовка Q3	Farrow & Ball No. 15 Farrow & Ball No. 34	31,85 7,46	Плинтус МДФ h=80 мм, аналог: МДФ под покраску 80×16	Farrow & Ball No. 15	16,2	Инженерная доска, 1167-4250, 2100×127 мм, на клею; тип 1, отм. ЧП ±0,000	17,89	Н стен 2700 (до потолка); плинтус в цвет: стены
2	Гардеробная-постирочная 5,11 м²	Окраска, Tikkurila Anti-Reflex 2, глубокоматовая, 2 слоя, подготовка Q3	Tikkurila V503	5,11	Окраска, Tikkurila Harmony, матовая, 2 слоя, подготовка Q3	Tikkurila V503	22,94	Плинтус МДФ h=80 мм, аналог: МДФ под покраску 80×16	Tikkurila V503	8,3	Инженерная доска, 1167-4250, 2100×127 мм, на клею; тип 1, отм. ЧП ±0,000	5,11	Н стен 2700 (до потолка); плинтус в цвет: стены
3	Кабинет 18,92 м²	Окраска, Tikkurila Anti-Reflex 2, глубокоматовая, 2 слоя, подготовка Q3	Tikkurila V503	18,92	Окраска, Farrow & Ball Modern Emulsion, матовая, 2 слоя, подготовка Q3 Акцент — стена А: окраска, Farrow & Ball Modern Emulsion, матовая, 2 слоя, подготовка Q3	Farrow & Ball No. 15 Farrow & Ball No. 34	35,80 5,78	Плинтус МДФ h=80 мм, аналог: МДФ под покраску 80×16	Farrow & Ball No. 15	16,7	Инженерная доска, 1167-4250, 2100×127 мм, на клею; тип 1, отм. ЧП ±0,000	18,92	Н стен 2700 (до потолка); плинтус в цвет: стены
4	Кухня-гостиная 45,51 м²	Окраска, Tikkurila Anti-Reflex 2, глубокоматовая, 2 слоя, подготовка Q3	Tikkurila V503	45,51	Окраска, Farrow & Ball Modern Emulsion, матовая, 2 слоя, подготовка Q3 Акцент — стена А: окраска, Farrow & Ball Modern Emulsion, матовая, 2 слоя, подготовка Q3 Фартук кухни (стена А): облицовка керамогранитом, аналог: керамогранит под травертин, матовый, 1200×600×9 мм, клей C2 TE S1, затирка CG2WA	Farrow & Ball No. 15 Farrow & Ball No. 34 по артикулу	48,70 15,64 0,70	Плинтус МДФ h=80 мм, аналог: МДФ под покраску 80×16	Farrow & Ball No. 15	25,9	Инженерная доска, 1167-4250, 2100×127 мм, на клею; тип 1, отм. ЧП ±0,000	45,51	Н стен 2700 (до потолка); матовая моющаяся, класс 1 EN 13300 — осознанно вместо полуматовой; плинтус в цвет: стены
5	Коридор 9,07 м²	Окраска, Tikkurila Anti-Reflex 2, глубокоматовая, 2 слоя, подготовка Q3	Tikkurila V503	9,07	Окраска, Farrow & Ball Modern Emulsion, матовая, 2 слоя, подготовка Q3	Farrow & Ball No. 15	33,47	Плинтус МДФ h=80 мм, аналог: МДФ под покраску 80×16	Farrow & Ball No. 15	11,2	Инженерная доска, 1167-4250, 2100×127 мм, на клею; тип 1, отм. ЧП ±0,000	9,07	Н стен 2700 (до потолка); матовая моющаяся, класс 1 EN 13300 — осознанно вместо полуматовой; плинтус в цвет: стены
6	Детская 9,97 м²	Окраска, Tikkurila Anti-Reflex 2, глубокоматовая, 2 слоя, подготовка Q3	Tikkurila V503	9,97	Окраска, Farrow & Ball Modern Emulsion, матовая, 2 слоя, подготовка Q3 Акцент — стена А: окраска, Farrow & Ball Modern Emulsion, матовая, 2 слоя, подготовка Q3	Farrow & Ball No. 15 Farrow & Ball No. 34	20,30 8,15	Плинтус МДФ h=69 мм, SX165	Farrow & Ball No. 15	12,0	Инженерная доска, 1167-4250, 2100×127 мм, на клею; тип 1, отм. ЧП ±0,000	9,97	Н стен 2700 (до потолка); плинтус в цвет: стены
7	Ванная 8,44 м²	Окраска, Tikkurila Luja 7, матовая, 2 слоя, подготовка Q3	Tikkurila V503	8,44	Облицовка плиткой, A8UZ, 600×1200×9 мм, клей C2 TE S1, затирка CG2WA	Atlas Concorde A8UZ	26,30	нет			Керамогранит, A8UZ, 600×1200×9 мм; тип 2, отм. ЧП −0,015	8,44	Н стен 2715 (до потолка); гидроизоляция обмазочная, 2 слоя, с заведением на стены 200 мм (по пирогу пола); тест проливом и акт скрытых работ
8	Прихожая 7,89 м²	Окраска, Tikkurila Anti-Reflex 2, глубокоматовая, 2 слоя, подготовка Q3	Tikkurila V503	7,89	Окраска, Farrow & Ball Modern Emulsion, матовая, 2 слоя, подготовка Q3	Farrow & Ball No. 15	21,53	Плинтус МДФ h=80 мм, аналог: МДФ под покраску 80×16	Farrow & Ball No. 15	7,0	Керамогранит, A8UZ, 600×1200×9 мм; тип 3, отм. ЧП ±0,000	7,89	Н стен 2700 (до потолка); матовая моющаяся, класс 1 EN 13300 — осознанно вместо полуматовой; плинтус в цвет: стены
9	Санузел гостевой 4,49 м²	Окраска, Tikkurila Luja 7, матовая, 2 слоя, подготовка Q3	Tikkurila V503	4,49	Облицовка плиткой, A8UZ, 600×1200×9 мм, клей C2 TE S1, затирка CG2WA	Atlas Concorde A8UZ	19,59	нет			Керамогранит, A8UZ, 600×1200×9 мм; тип 2, отм. ЧП −0,015	4,49	Н стен 2715 (до потолка); гидроизоляция обмазочная, 2 слоя, с заведением на стены 200 мм (по пирогу пола); тест проливом и акт скрытых работ
	Итого			**127,29**			**298,21**			**97,3**		**127,29**	

Примечания

1. Площади поверхностей — по чистым граням стен до отделки: стены = периметр × высоту от чистого пола помещения до низа потолка минус проёмы (облицовка плиткой — до верха облицовки); плинтус = периметр минус дверные проёмы; пол и потолок — по площади помещения. Количество плиток по раскладке. Площади помещений — с учётом всех частей помещения; откосы в площадь стен не входят.
2. Акцентные стены и фартук — отдельными строками, их площадь вычтена из основной отделки стен помещения; фартук — над нижними модулями кухни от столешницы до низа навесных шкафов, где шкафов нет — на 600 мм.
3. Плинтус — длина по периметру за вычетом дверных проёмов; примыкания к наличникам и встроенной мебели — по развёрткам.
4. Формат плитки — Ш×В×Т (ширина × высота в положении укладки × толщина), мм; на полу — вдоль стен А/В × вдоль стен Б/Г.
5. Коды цвета — по веерам производителей; колеровка каждой краски одной партией, проверка выкраса при свете D65 и при лампах проекта.
6. Уровни подготовки Q1–Q4 — система Knauf, не норма ГОСТ/СП; допуски поверхностей — по СП 71.13330.2017 (действующая редакция).
7. «аналог:» — изделие задано характеристиками, марку и артикул согласовать с заказчиком до закупки.

					Проект: Квартира с кабинетом			
	Лист	№ док.	Подпись	Дата	Ведомость отделки помещений	Стадия	Лист	Листов
Дизайнер	Кырлан А.С.			21.10.26		П	С1	97

Правка к этому листу

Поз.	Наименование и техническая характеристика	Тип, марка, обозначение документа	Код продукции	Поставщик	Ед. изм.	Кол.	Образец	Примечание
	Лакокрасочные материалы							
1	Краска интерьерная водно-дисперсионная акриловая для стен, матовая, класс мокрого истирания 1 по EN 13300, база A; цвет Farrow & Ball No. 15 «Bone — мягкий каменно-серый с зеленцой», колеровка машинная	Farrow & Ball Modern Emulsion		Farrow & Ball	л	52,5		поз. К1 колерной карты; пом. 1, 3, 4, 5, 6, 8; S = 191,7 м² × 2 сл. × 0,12 л/м² = 46,0 л, +10 % и 0,5 л на подкраску → ≥ 51,1 л; тара 10 × 5 л + 1 × 2,5 л
2	Краска интерьерная водно-дисперсионная акриловая для акцентных стен, матовая, класс мокрого истирания 1 по EN 13300, база C; цвет Farrow & Ball No. 34 «Calke Green — традиционный шалфей», колеровка машинная	Farrow & Ball Modern Emulsion		Farrow & Ball	л	12,5		поз. К2 колерной карты; пом. 1, 3, 4, 6; S = 37,0 м² × 2 сл. × 0,12 л/м² = 8,9 л, +10 % и 0,5 л на подкраску → ≥ 10,3 л; тара 2 × 5 л + 1 × 2,5 л
3	Краска интерьерная водно-дисперсионная акриловая для потолков, глубокоматовая, класс мокрого истирания 2 по EN 13300, база A; цвет Tikkurila V503 «Winter», колеровка машинная	Tikkurila Anti-Reflex 2		Tikkurila	л	31,5		поз. К3 колерной карты; пом. 1, 2, 3, 4, 5, 6, 8; S = 114,4 м² × 2 сл. × 0,12 л/м² = 27,4 л, +10 % и 0,5 л на подкраску → ≥ 30,7 л; тара 3 × 9 л + 1 × 2,7 л + 2 × 0,9 л
4	Краска интерьерная водно-дисперсионная акриловая для стен, матовая, класс мокрого истирания 1 по EN 13300, база A; цвет Tikkurila V503 «Winter», колеровка машинная	Tikkurila Harmony		Tikkurila	л	7,2		поз. К5 колерной карты; пом. 2; S = 22,9 м² × 2 сл. × 0,12 л/м² = 5,5 л, +10 % и 0,5 л на подкраску → ≥ 6,6 л; тара 2 × 2,7 л + 2 × 0,9 л
5	Краска интерьерная водно-дисперсионная акриловая для потолков, матовая, класс мокрого истирания 1 по EN 13300, база A; цвет Tikkurila V503 «Winter», колеровка машинная	Tikkurila Luja 7		Tikkurila	л	4,5		поз. К9 колерной карты; пом. 7, 9; S = 12,9 м² × 2 сл. × 0,12 л/м² = 3,1 л, +10 % и 0,5 л на подкраску → ≥ 3,9 л; тара 1 × 2,7 л + 2 × 0,9 л
6	Краска для МДФ и дерева в цвет Farrow & Ball No. 15 «Bone — мягкий каменно-серый с зеленцой» — окраска плинтуса; блеск не ниже блеска стен	марка не задана			л	2,3		поз. К4, К7; пом. 1, 3, 4, 5, 6, 8; L = 89,0 м, S = 8,4 м² × 2 сл. × 0,12 л/м² + 10 %; продукт подобрать в веере Farrow & Ball
7	Краска для МДФ и дерева в цвет Tikkurila V503 «Winter» — окраска плинтуса; блеск не ниже блеска стен	марка не задана			л	0,5		поз. К6; пом. 2; L = 8,3 м, S = 0,8 м² × 2 сл. × 0,12 л/м² + 10 %; продукт подобрать в веере Tikkurila
8	Грунтовка акриловая под окраску стен и потолков — из системы производителя краски	по системе краски			м²	379		площадь окраски стен, акцентов и потолков; 1 слой перед окраской; расход — по ТУ грунтовки
	Плитка и керамогранит							
9	Керамогранит под травертин, 600×600 мм	аналог по характеристикам			м²	18		шов 2 мм; Ванная, пол; Санузел гостевой, пол; по раскладке 45 шт (S = 12,93 м²), с запасом 50 шт
10	Керамогранит под травертин, 600×1200×9 мм, ректификат, водопоглощение 0,1 %	аналог по характеристикам		Atlas Concorde	м²	69,12		шов 2 мм; Ванная, стены А–Г; Ванная, короб инсталляции; Санузел гостевой, стены А–Г; Санузел гостевой, короб инсталляции; по раскладке 84 шт (S = 47,44 м²), с запасом 96 шт
11	A8UZ, 600×1200×9 мм, ректификат, водопоглощение 0,1 % (BIa), противоскольжение R10, PEI IV	A8UZ		Atlas Concorde	м²	12,24		шов 2 мм; Прихожая, пол; по раскладке 15 шт (S = 7,89 м²), с запасом 17 шт
12	Керамогранит под травертин, матовый, 1200×600×9 мм, ректификат, водопоглощение 0,1 % (BIa)	аналог по характеристикам			м²	2,16		шов 2 мм; Кухня-гостиная, фартук (ст. А); по раскладке 2 шт (S = 0,70 м²), с запасом 3 шт
	Напольные покрытия							
13	1167-4250, рабочий слой 4 мм, эмиссия E1, укладка на клей	1167-4250		Coswick	м²	114		пом. 1, 2, 3, 4, 5, 6; S = 106,47 м² + 7 % (прямая укладка); к заказу — кратно упаковке
14	Клей для паркета и инженерной доски, эластичный (СМП / полиуретановый)	по рекомендации производителя доски			м²	107		площадь приклейки; расход и шпатель — по ТУ клея
	Погонажные изделия							
15	Плинтус МДФ под покраску 80×16, крепление к стене, окраска в цвет Farrow & Ball No. 15	аналог по характеристикам			м	94		пом. 1, 2, 3, 4, 5, 8; L = 85,4 м (периметр без дверных проёмов) + 10 % на подрезку; в штуках — по длине планки
16	SX165, h = 69 мм, крепление к стене, окраска в цвет Farrow & Ball No. 15	SX165		Orac Decor	м	14		пом. 6; L = 12,0 м (периметр без дверных проёмов) + 10 % на подрезку; в штуках — по длине планки
	Смеси и материалы для облицовки							
17	Затирка для швов плитки, класс CG2WA по EN 13888	Mapei Ultracolor Plus 132		Mapei	кг	5,5		по раскладке (a+b)/(a·b) × шов × t × 1,6 + 10 %; в т. ч. 0,7 кг — позиции раскладки без марки
18	Клей плиточный C2 TE S1 по EN 12004, слой 5 мм	Ceresit CM 17		Ceresit	кг	543		22 меш. по 25 кг; 1,5 кг/м² на 1 мм слоя + 10 %; в т. ч. 70 кг — позиции раскладки без марки
19	Гидроизоляция обмазочная мокрых зон: пол, стены по периметру, зоны замачивания; 2 слоя с армирующей лентой в углах	аналог по характеристикам			м²	28,2		площадь по листу раскладки плитки + 10 %; расход смеси — по ТУ
20	Лента демпферная по периметру пола из плитки	аналог по характеристикам			м	28		периметр без дверных проёмов + 10 %

Примечания

1. Количества — из геометрии проекта: площади поверхностей по чистым граням стен до отделки (те же, что в ведомости отделки и колерной карте), плитка, клей и затирка — по раскладке плиточника; в графе «Кол.» — к заказу, с запасом.
2. Краска: расход 0,12 л/м² на слой в 2 слоя, если по ТУ не задан иной; запас 10 % и 0,5 л на подкраску каждого кода. Один код — одна партия, колеровка машинная в колеровочном центре бренда; в заказ — только после утверждения выкраса (колерная карта). Фасовка — по каталогу бренда на дату выпуска; к заказу — не меньше расчётного объёма.
3. «Аналог по характеристикам» — допускается изделие другого производителя с характеристиками не ниже указанных, по согласованию с автором проекта.
4. Графы «Код продукции» и «Масса 1 ед.» не заполнены: коды по классификатору продукции не присвоены, масса единицы до 25 кг (ГОСТ 21.110-2013).
5. Грунтовка и клей для доски указаны площадью обработки; объём — по ТУ выбранного продукта.


					Проект: Квартира с кабинетом
	Лист	№ док.	Подпись	Дата	Спецификация отделочных материалов
Дизайнер	Кырлан А.С.			21.10.26	

Стадия	Лист	Листов
П	С2	97

Правка к этому листу


1 Порог 15 мм: мокрая зона — жилое помещение (М 1:10)

Применение: двери Д-6, Д-7

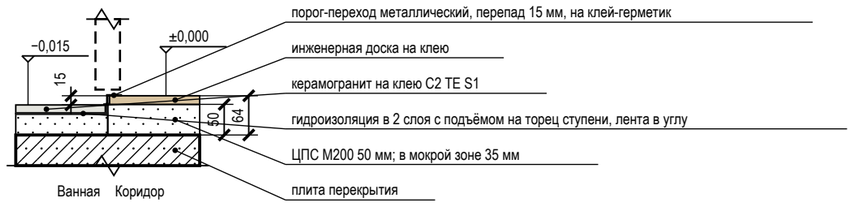


2 Дверь скрытого монтажа в плоскости стены, плинтус (М 1:5)

Применение: двери Д-2, Д-3, Д-4, Д-5, Д-6, Д-7

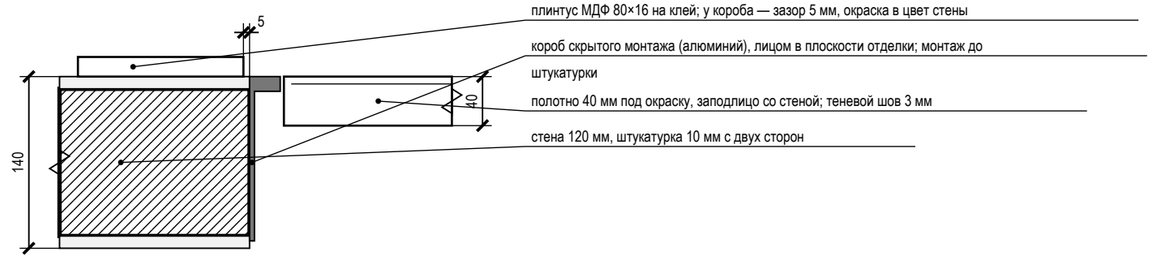


3 Короб стояков К1-1 с люком и звукоизоляцией (М 1:10)

Применение: пом. 9, 7, 4

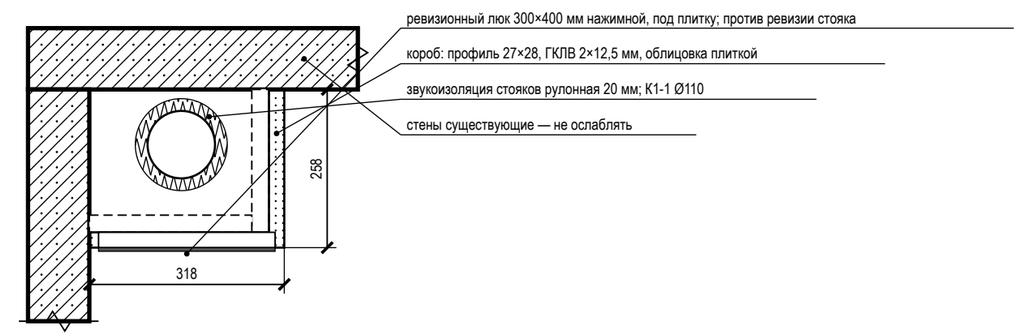


4 Гидроизоляция санузла: заход на стены 200 мм, примыкание ванны (М 1:20)

Применение: пом. 7, 9

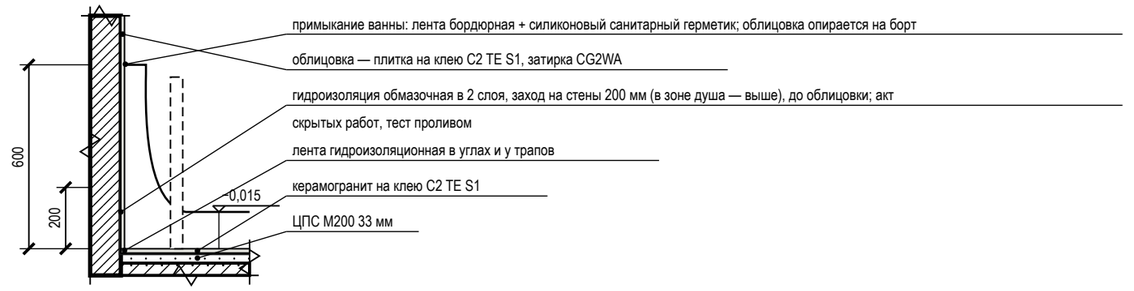

5 Плинтус МДФ 80×16 мм у окрашенной стены (М 1:10)

Применение: пом. 1, 2, 3, 4, 5, 6, 8

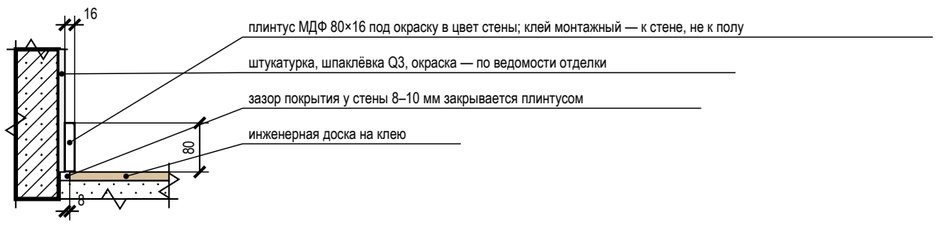

Условные обозначения

- железобетон (плита, стены)
- кладка, перегородка
- стяжка, раствор
- гипсокартон ГКЛВ
- звукоизоляция, эластичный заполнитель
- плитка, керамогранит на клею
- инженерная доска (покрытие пола)
- металлический профиль (порог, Т-профиль, короб двери)
- гидроизоляция (обмазочная, лента)

Примечания

1. Узлы — типовые решения проекта для мест, отмеченных выносками на листе схемы расположения развёрток и узлов; размеры — в мм, отметки — в м от ±0,000.
2. Узлы с гидроизоляцией, закладными и коробами скрытого монтажа принимаются по актам скрытых работ до закрытия отделкой; гидроизоляция — после теста проливом (24 ч).
3. Марки изделий (порог, Т-профиль, короб скрытой двери, люк) — по спецификациям; замена — на аналог с теми же габаритами по согласованию с автором проекта.

	Лист	№ док.	Подпись	Дата
Дизайнер	Кырлан А.С.			21.10.26

Проект: Квартира с кабинетом

Узлы

Стадия	Лист	Листов
П	С3	97

выпуск 18.10.2026 № 918b20bf25 · стр. 97 из 97