LINEA

ДИЗАЙН-ПРОЕКТ ИНТЕРЬЕРА

Квартира 68 м², элитный модерн



ПАЛИТРА ОТДЕЛКИ

F&B No. 2003	G503	F&B No. 34	F&B No. 281	F&B No. 43
51 %	30 %	6 %	4 %	4 %

АВТОР ПРОЕКТА

Кырлан Александр Сергеевич

Ноябрь 2026



Визуализация гостиной · 3D

ОБЩАЯ ПЛОЩАДЬ	ПОМЕЩЕНИЙ	СТАДИЯ	ШИФР	ОСНОВА
68,47 м²	7, из них жилых 3	Проект · предварительно	ГД-2026-020-АИ	план заказчика, без обмера

Как оставить правку: кнопка «Правка к этому листу» в правом верхнем углу любого листа · все листы проекта: дизайн-студия-квартир.рф/review.html?p=gost-elitemodern

выпуск 04.11.2026 № f0db2de63c · стр. 1 из 86

Объект

Квартира 68 м², элитный модерн: 68,47 м², помещений 7, из них жилых 3.

Стиль: современный (контемпорари) 60 %, тихая роскошь (quiet luxury) 40 %. Стадия: предварительный альбом без обмера, планировка по плану заказчика.

Открытых вопросов 25, конфликтов разделов 0; изменений утверждено 7, ждут подписи 0.

Розетки и выводы

56 розеток (рамок 44), 13 выводов кабеля под технику и свет, 20 групп щита — всё с высотами от чистого пола: листы 34, 35, 36.

Что решено (подписано вами)

ИЗ-1 — Решение автора: от чистого пола до плиты 2650 мм.

ИЗ-2 — Решение автора — по предложению исполнителя: кабинет у окна (бра 12), кухня-столовая с эркером (подсветка 13), гостиная, спальня (подвесы 13-А/13-Б, кровать 1800 между ними).

ИЗ-3 — Решение автора: большее — ванная (ванна 1700 у правой стены, умывальник на тумбе 800, стиральная машина 600 × 600 с выводами и розеткой на своей группе).

ИЗ-4 — Решение автора: все существующие стены — несущие до техзаключения.

ИЗ-5 — Решение: встраиваемые светильники тонкие, монтажная глубина ≤ 50 мм.

ИЗ-6 — Решение: вытяжная решётка на стене санузла и ванной в канал, вентилятор канальный настенный с обратным клапаном.

ИЗ-7 — Решение: допущение сохраняется — отметки дизайнера на 95 мм ниже чистого пола.

Что ждёт вашего ответа

К-1 — Планировка принята по обводу плана заказчика, без обмера: план заказчика распознан автоматически по картинке (1 модель ИИ, масштаб — размерные цепочки), затем исправлен…

К-3 — Тип дома, конструкция перекрытия и несущие стены в брифе не указаны.

К-4 — Стояки: на плане потолков есть только знак ∅ в верхнем левом углу ванной (120 мм от стены) — принят за стояк канализации К1 Ø110.

К-5 — Вентканалы в брифе не показаны: приняты у санузла и кухни.

К-6 — Разрешённая мощность по ТУ в брифе не указана.

К-7 — Стиль выбран заказчиком в брифе: Современный (модерн).

К-8 — Кухня, шкафы и встроенная техника описаны характеристиками («аналог по характеристикам»): модели не выбраны, ниши под технику — по паспорту выбранной модели.

К-9 — Состав семьи в брифе не указан (answers.household пуст): принято 2 человека.

К-10 — Заказчик указал в брифе, что плана нет и нужен обмер: все размеры альбома до обмера — допущение.

К-14 — Эркер кухни образмерен частично: окно 1300 мм, глубина ≈ 570 мм, скос к нижней стене ≈ 45° (на листе не образмерен, по рисунку ≈ 1150 мм, вероятно, тоже остеклён).

К-15 — В верхней (наружной?) стене кухни на плане два узких разрыва ≈ 130 мм (над лентой 13) с участком стены 650 мм между ними.

К-16 — Входная дверь на плане не помечена (марки Д-1…Д-5 — межкомнатные).

К-17 — Проём из прихожей в спальню (880 мм) без марки Д — это проём без двери или дверь, не попавшая в ведомость Д? Варианты: (1) дверь 800 с полотном, как остальные.

К-18 — В правом верхнем углу спальни прямоугольник ≈ 1300 × 290 мм вне контура потолка (без подписи): короб, шахта, пилон или шкаф.

и ещё 11 — на листе реестра

выпуск 04.11.2026 № f0db2de63c · стр. 2 из 86

					Проект: Квартира 68 м², элитный модерн
	Лист	№ док.	Подпись	Дата	Ваш проект на одной странице
Дизайнер	Кырлан А.С.			04.11.26	

Стадия	Лист	Листов
П	2	86



					Проект: Квартира 68 м², элитный модерн	
	Лист	№ док.	Подпись	Дата		
Дизайнер	Кырлан А.С.			04.11.26	Визуализация санузла	Стадия: П; Лист: 3; Листов: 86

Правка к этому листу

Список листов

Лист	Наименование
1	Титульный лист
2	Ваш проект на одной странице
3	Визуализация санузла
4	Список листов
5	Как читать альбом
6	План планировки (подобрана проектировщиком, плана заказчика нет)
7	План монтажный
8	Кухня (пом. 5). Монтажная схема
9	Шкафы. Монтажная схема
10	Карта покрытий стен
11	Колерная карта
12	План размещения мебели и оборудования
13	Спецификация мебели и оборудования
14	Спецификация мебели и оборудования (продолжение)
15	Спецификация мебели и оборудования (продолжение)
16	Ведомости изделий, техники и фурнитуры
17	План выводов сантехники
18	Схема разводки водопровода и канализации
19	Аксонометрическая схема В1 (холодное водоснабжение)
20	Аксонометрическая схема Т3 (горячее водоснабжение)
21	Аксонометрическая схема К1 (канализация)
22	Развёртки мокрых зон: выводы ВК. Санузел
23	Развёртки мокрых зон: выводы ВК. Ванная (лист 1 из 2)
24	Развёртки мокрых зон: выводы ВК. Ванная (лист 2 из 2)
25	Развёртки мокрых зон: выводы ВК. Кухня-столовая
26	Спецификация сантехнического оборудования
27	Раскладка плитки. Санузел. Развёртки стен
28	Раскладка плитки. Ванная. Развёртки стен
29	План размещения дверей
30	План потолков
31	Разрезы и узлы потолков
32	Разрезы и узлы потолков (продолжение)
33	Сечения потолков М 1:10
34	Однолинейная схема щита
35	Однолинейная схема щита (продолжение)
36	План розеток и электровыводов
37	План слаботочных сетей
38	План освещения
39	Техническое задание на подбор светильников
40	Управление светильниками
41	План вентиляции
42	План отопления
43	План покрытий пола
44	Раскладка плитки. Планы полов
45	Раскладка плитки. Фартук кухни
46	Развёртка стены А. Кабинет (пом. 1)
47	Привязки электроточек, стена А. Кабинет (пом. 1)
48	Развёртка стены Б. Кабинет (пом. 1)
49	Развёртка стены В. Кабинет (пом. 1)
50	Развёртка стены Г. Кабинет (пом. 1)
51	Развёртки стен А, Б, В. Санузел (пом. 2)
52	Развёртка стены Г. Санузел (пом. 2)
53	Привязки электроточек и выводов ВК, стена Г. Санузел (пом. 2)
54	Развёртки стен А, Б. Ванная (пом. 3)
55	Развёртки стен В, Г. Ванная (пом. 3)
56	Привязки электроточек и выводов ВК, стена Г. Ванная (пом. 3)
57	Развёртка стены А. Прихожая (пом. 4)
58	Развёртка стены Б. Прихожая (пом. 4)
59	Развёртка стены В. Прихожая (пом. 4)
60	Развёртка стены Г. Прихожая (пом. 4)
61	Привязки электроточек, стена Г. Прихожая (пом. 4)
62	Развёртка стены А1. Кухня-столовая (пом. 5), кухонный фронт
63	Привязки электроточек и выводов ВК, стена А1. Кухня-столовая (пом. 5)
64	Развёртки стен А2, Б1, Б2. Кухня-столовая (пом. 5)
65	Развёртка стены В. Кухня-столовая (пом. 5)
66	Развёртка стены Г. Кухня-столовая (пом. 5)
67	Развёртка стены А. Гостиная (пом. 6)
68	Привязки электроточек, стена А. Гостиная (пом. 6)
69	Развёртка стены Б. Гостиная (пом. 6)
70	Развёртка стены В. Гостиная (пом. 6)
71	Развёртка стены Г. Гостиная (пом. 6)
72	Развёртки стен А1, А2. Спальня (пом. 7)
73	Развёртки стен Б, Г. Спальня (пом. 7)
74	Развёртка стены В. Спальня (пом. 7)
75	Привязки электроточек, стена В. Спальня (пом. 7)
76	Открытые вопросы, принятые допущения и конфликты. Лист 1 из 3
77	Открытые вопросы, принятые допущения и конфликты. Лист 2 из 3
78	Открытые вопросы, принятые допущения и конфликты. Лист 3 из 3
Д_1	Шкаф-купе М_03
Д_2	Кухня (пом. 5). Развёртка гарнитура
С1	Ведомость отделки помещений. Лист 1 из 2
С2	Ведомость отделки помещений. Лист 2 из 2
С3	Спецификация отделочных материалов
С4	Список покупок
С5	Список покупок (окончание)
С6	Узлы

Общие указания

1. Размеры даны в мм от чистовых поверхностей стен: слой штукатурки 20 мм по блоку и 5 мм шпаклёвки по ГКЛ учтён. Перед заказом встроенной мебели — контрольный обмер после штукатурки.
2. Привязки мебели — от стен и углов помещения, а не от другой мебели.
3. Розетки, выводы и выключатели под мебель — см. лист 36 «План розеток и электровыводов»; сантехприборы и выводы воды — лист 17.
4. План расстановки не является документацией для изготовления мебели: изделия — по чертежам мебельщика; покупную мебель заменять только на изделия не больше габарита из спецификации (лист 13).
5. Встроенная мебель «стена в стену» — с зазором 10 мм с каждой стороны или с компенсаторами.
6. Развёртки — вид на стену изнутри помещения, по часовой стрелке; расположение стен на схеме листа развёртки; размеры — в мм по чистовым поверхностям; отметки — в м от ±0,000; высоты Н — от чистого пола помещения до оси изделия, у декора — до центра.
7. Красная цепочка — привязки электроточек и выводов по осям от угла чистовых стен; высота Н — у знака, от чистого пола до оси; высоты мебели, проёмов и границ отделки колонкой отметок слева. Стена с 5 и более точками или с мелкими звеньями привязок показана двумя видами: архитектурная развёртка (мебель, отделка, проёмы, высоты) и вид «Привязки» на отдельном листе — точки и выводы с марками, одна цепочка по осям и таблица привязок (каждая точка — строка).
8. У знака электроточки: марка (Р — розетка, S — выключатель, Св — светильник, ЭВ вывод кабеля), ×N — число постов в рамке, гр. — группа щита, Н — высота оси от чистого пола, мм; группы по клавишам выключателя — на листе выключателей.
9. Схема мебели, приборов и декора не является технической документацией для производства мебели; габариты — по паспортам изделий.
10. Марки позиций: М_NN — мебель, ОБ_NN — оборудование, С_NN — сантехника; О-N отделка (ведомость отделочных материалов, серия С).
11. Размеры мебели и изделий на заказ уточнить по месту после отделочных работ.

					Проект: Квартира 68 м², элитный модерн
	Лист	№ док.	Подпись	Дата	
Дизайнер	Кырлан А.С.			04.11.26	Список листов
					Стадия: П; Лист: 4; Листов: 86

выпуск 04.11.2026 № f0db2de63c · стр. 4 из 86

Что в альбоме

Альбом — дизайн-проект с рабочими чертежами для ремонта. Листы идут в порядке работ: титул и вводные, реестр открытых вопросов и решений, планы (обмер, монтаж стен, мебель, двери, потолки, полы), инженерия (сантехника, электрика, вентиляция и отопление), развёртки стен с визуализациями помещений, чертежи мебели, ведомости материалов и узлы.

Вам как заказчику — титул, эта вводная, «Ваш проект на одной странице», реестр вопросов, план мебели, визуализации и развёртки, ведомости мебели и материалов. Подрядчику — всё остальное: монтажные планы, привязки выводов и розеток, узлы, ведомости объёмов.

Знаки на листах

Без знака — решение утверждено или подтверждено обмером.

Что проверить до ремонта

1. Розетки у кровати и рабочего места: хватает ли их с каждой стороны кровати и над столом (план розеток — лист 36).

2. Выводы под технику — варочная панель, духовка, посудомойка, стиральная машина, бойлер: совпадают ли с выбранными моделями (листы 13, 14, 15, 36).

3. Высоты розеток, выключателей и выводов даны от чистого пола: если мебель или техника будут другими — скажите до штробления стен.

Номера записей

К-N — открытый вопрос: чего не хватает или что выбрать (варианты и рекомендация — в тексте). Пока ответа нет, действует строка «если решения нет».

Кф-N — конфликт между разделами (например, мебель и радиатор в одном месте); закрывается решением, которое записывается как ИЗ-N.

ИЗ-N — изменение проекта: что было, что стало и кто утвердил. Изменение без подписи предложение.


Все записи — на листе реестра сразу после вводных; на других листах на них стоят ссылки.

Почему альбом предварительный

Обмера на объекте не было: размеры взяты с плана заказчика. Технические условия (мощность, вода, вентиляция дома) не получены, часть решений ждёт вашего ответа. Пока в реестре есть открытые вопросы, альбом предварительный — пометка в штампе снимается закрытием вопросов, а не стиранием.

Правку к любому листу можно оставить по кнопке «Правка к листу» или на сайте студии: дизайн-студия-квартир.рф — укажите номер листа и что изменить.

3 круга правок входят в цену; условия — в договоре и на странице вашего заказа на сайте студии.

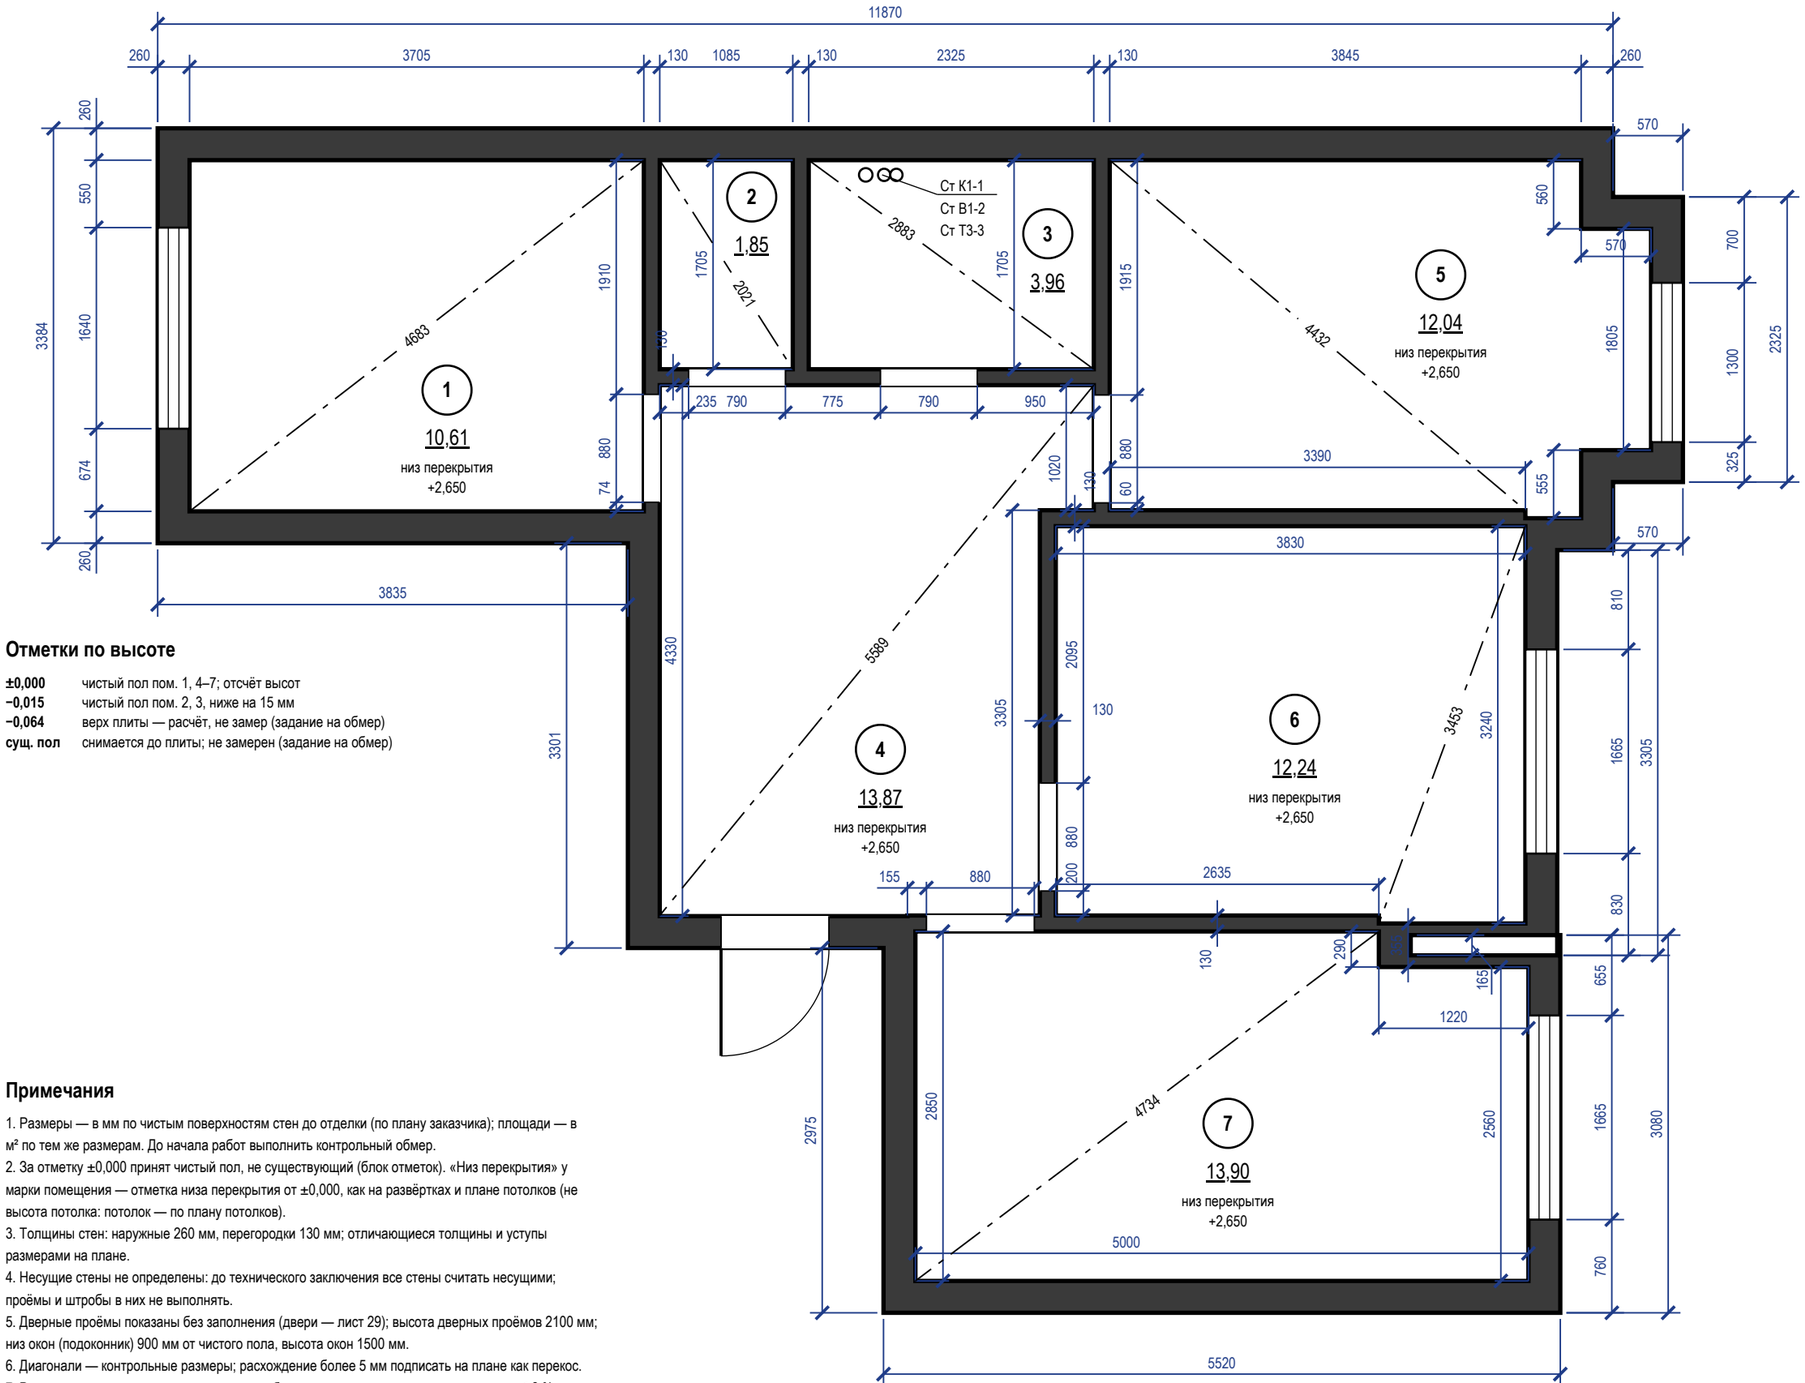

Экспликация помещений

№	Наименование	Площадь, м²
1	Кабинет	10,61
2	Санузел	1,85
3	Ванная	3,96
4	Прихожая	13,87
5	Кухня-столовая	12,04
6	Гостиная	12,24
7	Спальня	13,90
	Итого (общая площадь)	**68,47**

Условные обозначения

- существующие стены (сечение)
- окно (рама, остекление)
- проём существующий, без заполнения (откосы)
- стояк: К1 — канализация, В1 — ХВС, Т3 — ГВС
- диагональ помещения — контроль прямоугольности
- (1) номер помещения, площадь м²

Отметки по высоте


±0,000	чистый пол пом. 1, 4–7; отсчёт высот
−0,015	чистый пол пом. 2, 3, ниже на 15 мм
−0,064	верх плиты — расчёт, не замер (задание на обмер)
сущ. пол	снимается до плиты; не замерен (задание на обмер)

Примечания

1. Размеры — в мм по чистым поверхностям стен до отделки (по плану заказчика); площади — в м² по тем же размерам. До начала работ выполнить контрольный обмер.
2. За отметку ±0,000 принят чистый пол, не существующий (блок отметок). «Низ перекрытия» у марки помещения — отметка низа перекрытия от ±0,000, как на развёртках и плане потолков (не высота потолка: потолок — по плану потолков).
3. Толщины стен: наружные 260 мм, перегородки 130 мм; отличающиеся толщины и уступы размерами на плане.
4. Несущие стены не определены: до технического заключения все стены считать несущими; проёмы и штробы в них не выполнять.
5. Дверные проёмы показаны без заполнения (двери — лист 29); высота дверных проёмов 2100 мм; низ окон (подоконник) 900 мм от чистого пола, высота окон 1500 мм.
6. Диагонали — контрольные размеры; расхождение более 5 мм подписать на плане как перекос.
7. Размеры проверить на месте до начала работ; расхождение контрольных промеров ≤ 2 %.
8. Размеры короче 1 мм на листе цепочкой не показаны (две выносные линии на таком расстоянии сливаются): пом. 4, стена В — 45 мм от проёма до угла.

					Проект: Квартира 68 м², элитный модерн	**М 1:50**
	Лист	№ док.	Подпись	Дата	План планировки (подобрана проектировщиком, плана заказчика нет)	Стадия / Лист / Листов
Дизайнер	Кырлан А.С.			04.11.26		П / 6 / 86

выпуск 04.11.2026 № f0db2de63c · стр. 6 из 86

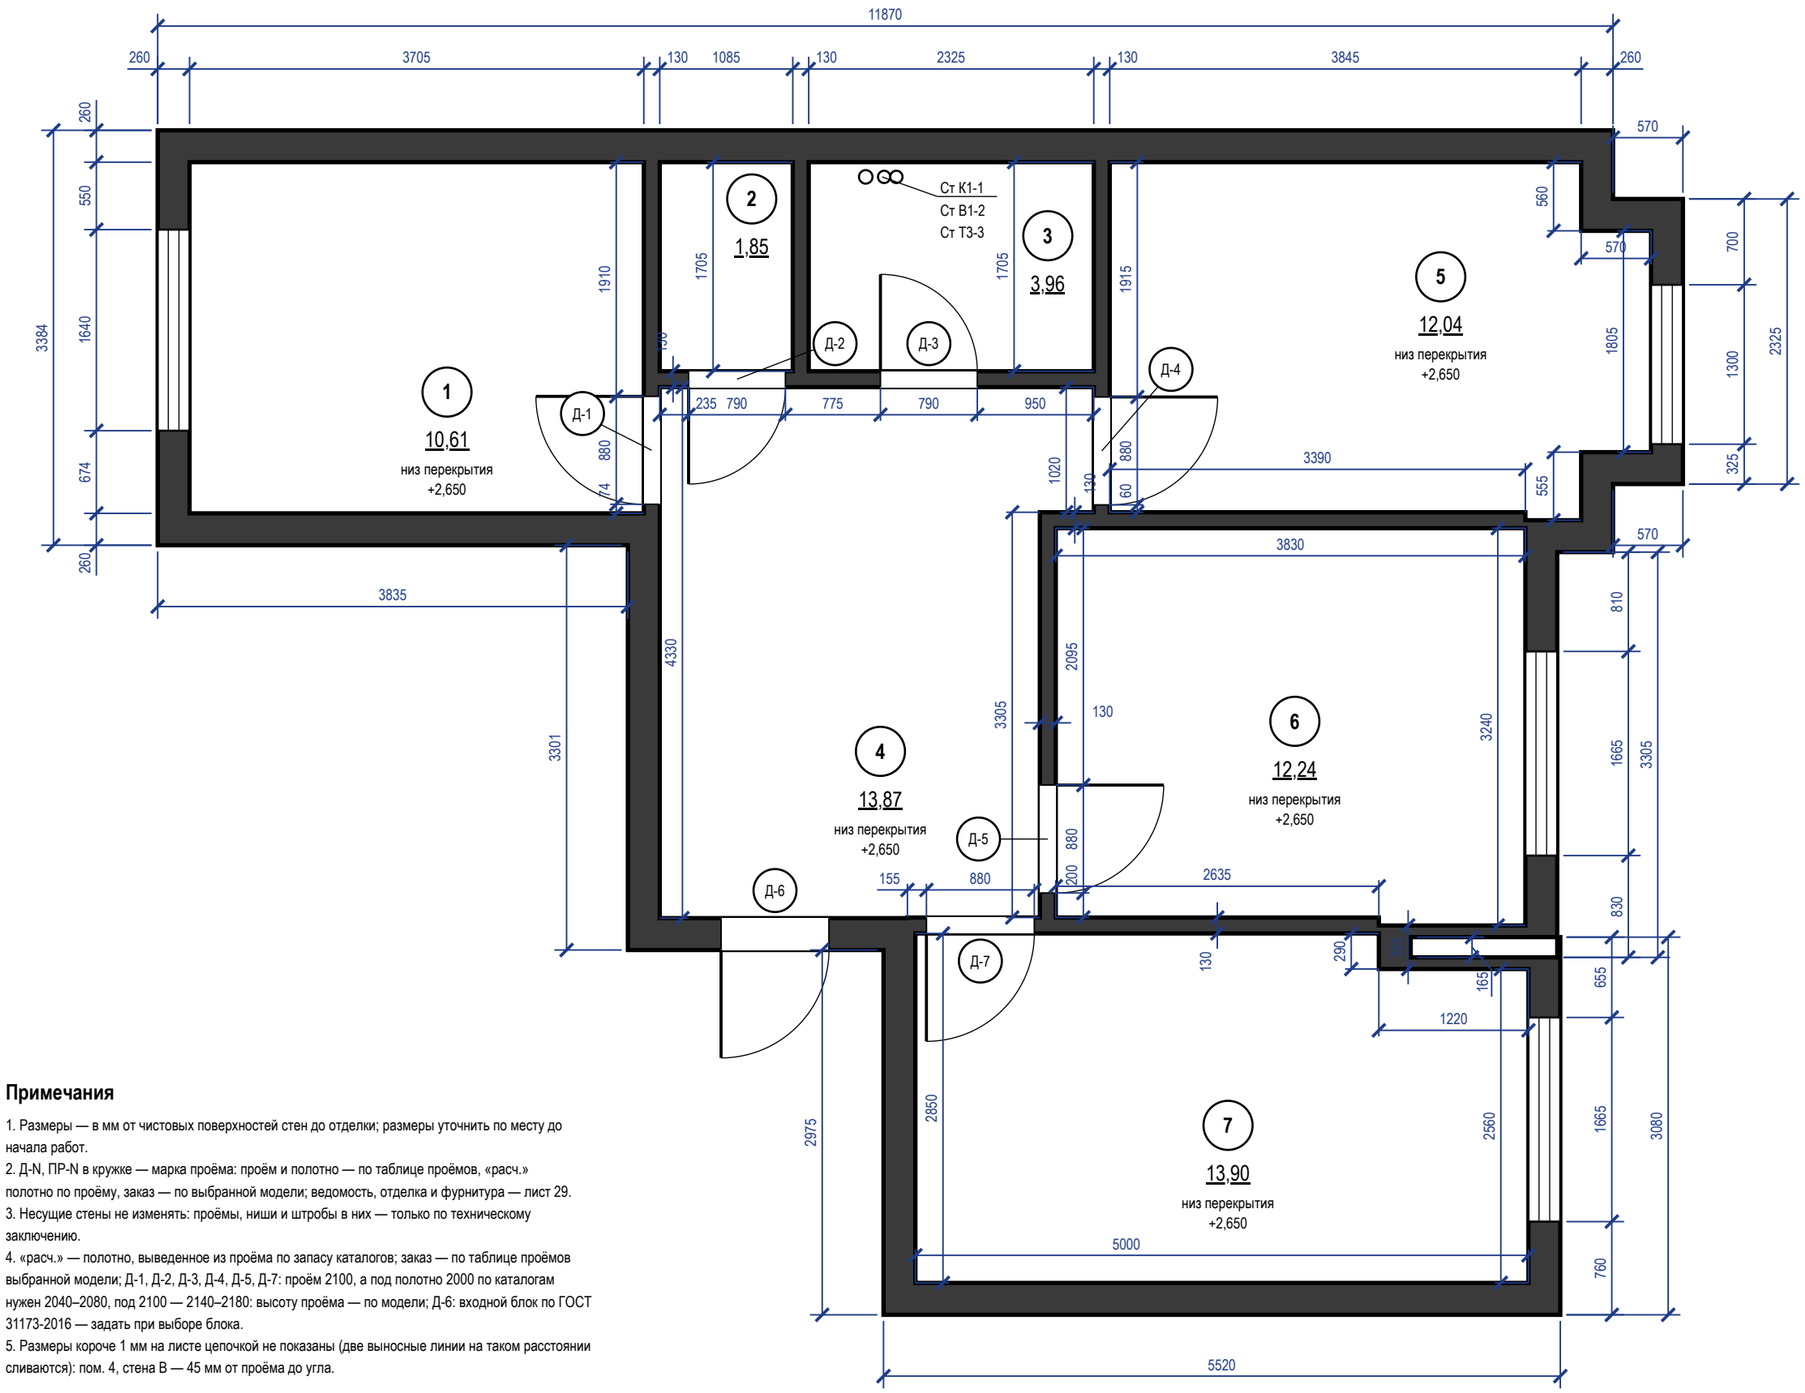

Экспликация помещений

№	Наименование	Площадь, м²
1	Кабинет	10,61
2	Санузел	1,85
3	Ванная	3,96
4	Прихожая	13,87
5	Кухня-столовая	12,04
6	Гостиная	12,24
7	Спальня	13,90
	Итого (общая площадь)	**68,47**

Таблица проёмов

Марка	Наименование	Проём ш×в, мм	Полотно (расч.)
Д-1	Дверь распашная	880×2100	800×2000
Д-2	Дверь распашная	790×2100	700×2000
Д-3	Дверь распашная	790×2100	700×2000
Д-4	Дверь распашная	880×2100	800×2000
Д-5	Дверь распашная	880×2100	800×2000
Д-6	Дверь входная	880×2100	блок — задать
Д-7	Дверь распашная	880×2100	800×2000

Примечания

1. Размеры — в мм от чистовых поверхностей стен до отделки; размеры уточнить по месту до начала работ.
2. Д-N, ПР-N в кружке — марка проёма: проём и полотно — по таблице проёмов, «расч.» полотно по проёму, заказ — по выбранной модели; ведомость, отделка и фурнитура — лист 29.
3. Несущие стены не изменять: проёмы, ниши и штробы в них — только по техническому заключению.
4. «расч.» — полотно, выведенное из проёма по запасу каталогов; заказ — по таблице проёмов выбранной модели; Д-1, Д-2, Д-3, Д-4, Д-5, Д-7: проём 2100, а под полотно 2000 по каталогам нужен 2040–2080, под 2100 — 2140–2180: высоту проёма — по модели; Д-6: входной блок по ГОСТ 31173-2016 — задать при выборе блока.
5. Размеры короче 1 мм на листе цепочкой не показаны (две выносные линии на таком расстоянии сливаются): пом. 4, стена В — 45 мм от проёма до угла.

	Лист	№ док.	Подпись	Дата
Дизайнер	Кырлан А.С.			04.11.26


Проект: Квартира 68 м², элитный модерн — **М 1:50**

План монтажный


Стадия	Лист	Листов
П	7	86

выпуск 04.11.2026 № f0db2de63c · стр. 7 из 86

Привязка выводов и крепление модулей

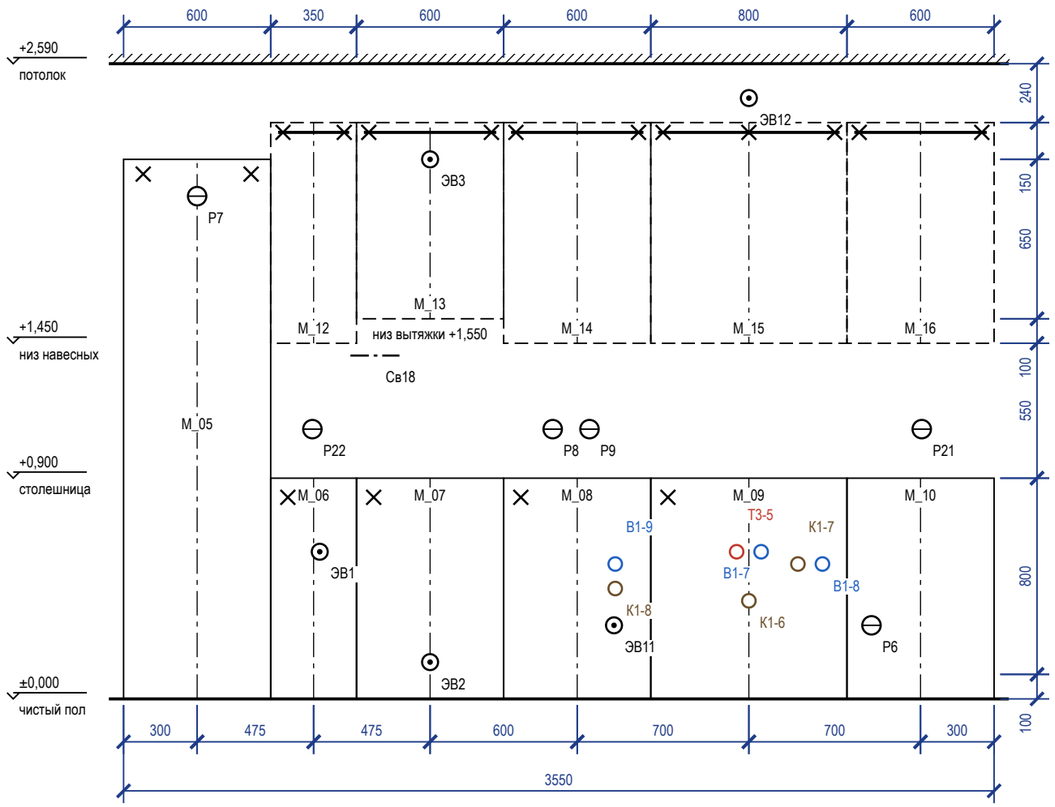

План столешницы

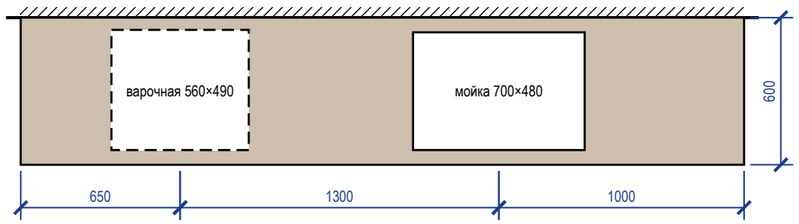

Примечания

1. Выводы — по проекту электрики и ВК; привязка по горизонтали — от оси модуля (плюс — вправо по виду), по высоте — от чистого пола до оси вывода.
2. Пенал — уголки к стене 2 шт. сверху; нижние модули — стяжками между собой и уголком к стене; ряд выставить по уровню опорами цоколя.
3. Розетки над столешницей — не ниже 150 мм над ней и не за корпусом техники; розетка за ПММ, духовым шкафом и холодильником — только в соседнем модуле или в зоне цоколя с доступом.
4. Столешница — вырезы по шаблонам выбранных моделей мойки и варочной панели; торцы у стены — герметик, пристеночный плинтус.

Условные обозначения

- нижний модуль, пенал (контур)
- невидимый контур: навесной модуль, корпус под столешницей
- ось модуля (от неё — привязка вывода)
- анкер / уголок крепления к стене
- розетка на стене
- вывод кабеля к технике
- B1 — вывод воды В1 / Т3, канализации К1

Привязка выводов к осям модулей

Код	Назначение	Модуль	От оси, мм	Н, мм	Размещение
Р7	розетка — холодильник — над нишей, съёмная панель	М_05	0	2050	над нишей холодильника, съёмная панель
Р22	розетка ×2 — фартук	М_06	−5	1100	над столешницей (фартук)
ЭВ1	вывод кабеля — варочная панель — в соседнем модуле, за ящиком	М_06	+25	600	в соседнем модуле, за ящиком
Св18	светодиодная лента — марка 13 по исходному плану: «підсвітка робочої поверхні»	М_07	−225	1400	над столешницей (фартук)
ЭВ2	вывод кабеля — духовой шкаф — в цоколе	М_07	0	150	под духовым шкафом, доступ через ящик
ЭВ3	вывод кабеля — вытяжка — над корпусом	М_13	0	2200	в навесном модуле
Р8	розетка ×2 — чайник и кофемашина (отдельная линия)	М_08	−100	1100	над столешницей (фартук)
Р9	розетка — фартук: мелкая техника	М_08	+50	1100	над столешницей (фартук)
ЭВ11	вывод кабеля — измельчитель мойки	М_08	+150	300	в соседнем модуле, за ящиком
В1-9	В1 — ro-filter	М_08	+155	550	в соседнем модуле, за ящиком
К1-8	К1 Ø40 — ro-filter	М_08	+155	450	в соседнем модуле, за ящиком
Т3-5	Т3 — межос. 100	М_09	−50	600	в модуле мойки
ЭВ12	вывод кабеля — подсветка навесных шкафов (блок питания ленты)	М_15	0	2450	в навесном модуле
К1-6	К1 Ø50 — мойка	М_09	0	400	в модуле мойки
В1-7	В1 — межос. 100	М_09	+50	600	в модуле мойки
К1-7	К1 Ø40 — слив ПММ в шкафу мойки	М_09	+200	550	в модуле мойки
В1-8	В1 — кран ПММ в шкафу мойки	М_09	+300	550	в модуле мойки
Р6	розетка — посудомоечная машина (в нише М_10, сбоку от корпуса, доступ через цоколь)	М_10	−200	300	за ПММ — перенести в соседний модуль
Р21	розетка ×2 — фартук	М_10	+5	1100	над столешницей (фартук)


Зазоры под отделку

Поверхность	Отделка	Зазор, мм	Учесть
фартук	керамогранит	10	от чернового основания до корпуса навесных и столешницы
стены	окраска	5	под штукатурку и шпаклёвку за пеналом
пол	инженерная доска		цоколь — после укладки пола, опоры ±20 мм

					Проект: Квартира 68 м², элитный модерн — М 1:25
	Лист	№ док.	Подпись	Дата	
Дизайнер	Кырлан А.С.			04.11.26	Кухня (пом. 5). Монтажная схема
					Стадия: П; Лист: 8; Листов: 86

выпуск 04.11.2026 № f0db2de63c · стр. 8 из 86

Шкаф-купе М_03 (пом. 4)

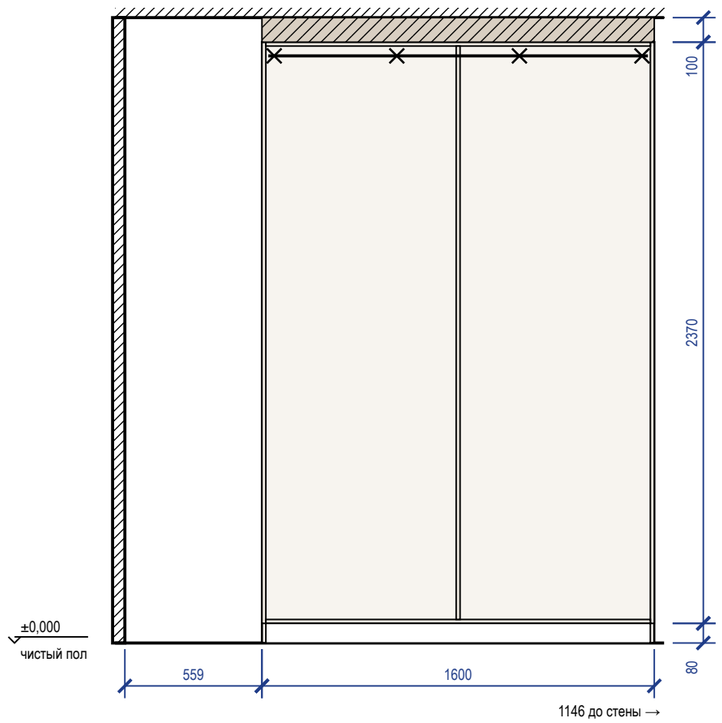

Крепление и зазоры под отделку

Марка	Помещение, стена	Основание	Отделка стены	Зазор, мм	Крепёж по планке	От опрокидывания
М_03	Прихожая (4), стена Б	по основанию — см. таблицу крепежа	окраска	5	анкер 4 шт., шаг 500	уголки 2 шт.

Крепёж по основанию стены

Основание стены	Крепёж
бетон, ж/б	анкер-шуруп 7,5×72 или дюбель 8×60 с шурупом 5×70
кирпич полнотелый	дюбель 8×80 с шурупом 5×90
газобетон, пазогребень	дюбель для газобетона 10×100 или химический анкер
гипсокартон	закладная до обшивки (брус 40×80 или фанера 18 мм), саморез в закладную

Условные обозначения

- анкер / уголок крепления к стене
- корпус и полки ЛДСП (вид на стену)
- компенсатор — короб до потолка

Примечания

1. Установочные размеры — от чистого пола и чистых стен; перед установкой контрольный замер после отделки.
2. Порядок: корпус выставить по уровню опорами цоколя → закрепить к стене по задней планке → навесить двери и фасады, отрегулировать зазоры → подогнать и закрепить компенсатор.
3. Анкеры — с шагом не более 500 мм, не ближе 50 мм от края планки; на ГКЛ только в закладную, установленную до обшивки.
4. Скрытые коммуникации под анкеры проверить детектором; трассы электрики по плану розеток.

					Проект: Квартира 68 м², элитный модерн	М 1:25
	Лист	№ док.	Подпись	Дата		
Дизайнер	Кырлан А.С.			04.11.26	Шкафы. Монтажная схема	Стадия: П; Лист: 9; Листов: 86



Покрытия стен

Марка	Покрытие	Помещение: S, м²	Итого, м²
O1	окраска Farrow & Ball · No. 2003 «Pointing»	1: 19,9; 4: 26,5; 5: 22,3; 6: 22,1; 7: 25,7	116,6
O2	окраска Tikkurila · No. 30 «Hague Blue — глубокий сине-зелёный»	1: 9,5	9,5
O6	облицовка плиткой · 600×1200 мм	2: 11,3; 3: 17,3	28,5
O10	окраска Tikkurila · No. 281 «Stiffkey Blue — чернильный синий»	5: 9,9	9,9
O11	окраска Farrow & Ball · No. 43 «Eating Room Red — брусничный красный»	6: 9,8	9,8
O12	окраска Farrow & Ball · No. 34 «Calke Green — традиционный шалфей»	7: 10,0	10,0

Площади — нетто, по развёрткам (за вычетом проёмов и фартука); высоты помещений — от чистого пола.

					Проект: Квартира 68 м², элитный модерн — **М 1:50**
	Лист	№ док.	Подпись	Дата	
Дизайнер	Кырлан А.С.			04.11.26	Карта покрытий стен
					Стадия: П; Лист: 10; Листов: 86

выпуск 04.11.2026 № f0db2de63c · стр. 10 из 86

Колерная карта по помещениям

Помещение	Поверхность	Образец	Поз.	Система и код цвета	Производитель, линейка / материал, артикул	Блеск	Класс истирания	LRV	Площадь
1. Кабинет 10,61 м²	стены		**К1**	Farrow & Ball No. 2003	Farrow & Ball · Modern Emulsion	матовая	1	86	20,1 м²
	акцент В		**К2**	Farrow & Ball No. 30	Tikkurila · Euro Power 7, колеровка по NCS	матовая	1	7	9,6 м²
	потолок		**К3**	Tikkurila G503	Tikkurila · Euro Power 7	глубокомат.	2	89	10,6 м²
	пол		**КМ1**	по образцу	инженерная доска · аналог по хар.				10,6 м²
	плинтус		**К4**	Farrow & Ball No. 2003	МДФ · в цвет Farrow & Ball			86	12,3 м
2. Санузел 1,85 м²	стены		**КМ2**	по образцу	плитка · аналог по хар.				11,8 м²
	потолок		**К5**	Tikkurila G503	Tikkurila · Euro Power 7	матовая	1	89	1,9 м²
	пол		**КМ3**	по образцу	керамогранит · аналог по хар.				1,9 м²
3. Ванная 3,96 м²	стены		**КМ2**	по образцу	плитка · аналог по хар.				17,7 м²
	потолок		**К5**	Tikkurila G503	Tikkurila · Euro Power 7	матовая	1	89	4,0 м²
	пол		**КМ3**	по образцу	керамогранит · аналог по хар.				4,0 м²
4. Прихожая 13,87 м²	стены		**К1**	Farrow & Ball No. 2003	Farrow & Ball · Modern Emulsion	матовая	1	86	27,6 м²
	потолок		**К3**	Tikkurila G503	Tikkurila · Euro Power 7	глубокомат.	2	89	13,9 м²
	пол		**КМ4**	по образцу	керамогранит · аналог по хар.				13,9 м²
	плинтус		**К4**	Farrow & Ball No. 2003	МДФ · в цвет Farrow & Ball			86	9,8 м
5. Кухня-столовая 12,04 м²	стены		**К1**	Farrow & Ball No. 2003	Farrow & Ball · Modern Emulsion	матовая	1	86	22,6 м²
	акцент В		**К6**	Farrow & Ball No. 281	Tikkurila · Euro Power 7, колеровка по NCS	матовая	1	10.1	10,0 м²
	потолок		**К3**	Tikkurila G503	Tikkurila · Euro Power 7	глубокомат.	2	89	12,0 м²
	пол		**КМ1**	по образцу	инженерная доска · аналог по хар.				12,0 м²
	плинтус		**К4**	Farrow & Ball No. 2003	МДФ · в цвет Farrow & Ball			86	13,8 м
	фартук		**КМ5**	по образцу	керамогранит · аналог по хар.				1,7 м²
6. Гостиная 12,24 м²	стены		**К1**	Farrow & Ball No. 2003	Farrow & Ball · Modern Emulsion	матовая	1	86	22,4 м²
	акцент А		**К7**	Farrow & Ball No. 43	Farrow & Ball · Modern Emulsion	матовая	1	11.8	9,9 м²
	потолок		**К3**	Tikkurila G503	Tikkurila · Euro Power 7	глубокомат.	2	89	12,2 м²
	пол		**КМ1**	по образцу	инженерная доска · аналог по хар.				12,2 м²
	плинтус		**К4**	Farrow & Ball No. 2003	МДФ · в цвет Farrow & Ball			86	13,3 м
7. Спальня 13,9 м²	стены		**К1**	Farrow & Ball No. 2003	Farrow & Ball · Modern Emulsion	матовая	1	86	23,4 м²
	акцент В		**К8**	Farrow & Ball No. 34	Farrow & Ball · Modern Emulsion	матовая	1	22	12,9 м²
	потолок		**К3**	Tikkurila G503	Tikkurila · Euro Power 7	глубокомат.	2	89	13,9 м²
	пол		**КМ1**	по образцу	инженерная доска · аналог по хар.				13,9 м²
	плинтус		**К4**	Farrow & Ball No. 2003	МДФ · в цвет Farrow & Ball			86	14,8 м

Перечень выкрасов на согласование

№	Код	Бренд / веер	Пом. / стена	Подложка	Формат	Статус
1	No. 2003	Farrow & Ball	1, 4, 5, 6, 7	ГКЛ с грунтом; МДФ под эмаль	600×1000; 300×600	к выполнению
2	No. 30	Farrow & Ball	1 В	ГКЛ с грунтом	600×1000	к выполнению
3	G503	Tikkurila	1, 2, 3, 4, 5, 6, 7	ГКЛ с грунтом	600×1000	к выполнению
4	No. 281	Farrow & Ball	5 В	ГКЛ с грунтом	600×1000	к выполнению
5	No. 43	Farrow & Ball	6 А	ГКЛ с грунтом	600×1000	к выполнению
6	No. 34	Farrow & Ball	7 В	ГКЛ с грунтом	600×1000	к выполнению

Примечания

1. Цвет на листе и на экране — ориентир. До покраски — выкрас на объекте: не меньше А3 (или лист ГКЛ), на грунте под эту краску, не на белой шпаклёвке, в 2 слоя; на обороте — код, бренд, веер, дата. Смотреть днём и вечером, рядом с образцами пола и плитки; к основному цвету стен — ещё 2 соседних оттенка. Красить только в цвет утверждённого выкраса.
2. Краску заказывать по коду из графы «Система и код цвета» у бренда этого кода, не «аналогом» другого; весь объём одного кода — одной партией, колеруемую краску — за один проход машины.
3. Площади — те же, что в ведомости отделки (лист С1); сколько краски заказать — в спецификации отделочных материалов (лист С3).

Схема квартиры: цвет стен и акценты (б/м)

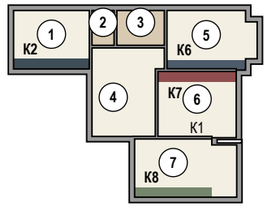


Схема палитры проекта


Стиль: Современный (контемпорари) 60% + Тихая роскошь (quiet luxury) 40% · схема: комплементарная

основной	основной	основной	второстепенный	второстепенный	второстепенный	акцентный	акцентный	акцентный	акцентный	акцентный	акцентный	акцентный	акцентный
Tikkurila G503	Farrow & Ball No. 2003	Tikkurila V503	Farrow & Ball No. 231	NCS S 2010-Y30R	Tikkurila H497	NCS S 7010-Y50R	NCS S 6020-G70Y	Farrow & Ball No. 228	Farrow & Ball No. 43	Farrow & Ball No. 30	Farrow & Ball No. 281	Farrow & Ball No. 43	Farrow & Ball No. 34
Calla LRV 89 потолок 1,2,3,4,5,6,7; текстиль/декор 1,6,7	Pointing LRV 86 стены 1,4,5,6,7; плинтус 1,4,5,6,7	Winter LRV 86 в отделке не применён	Shaded White LRV 63 текстиль/декор 1,5,6,7	светлый кэмел LRV 60 текстиль/декор 6,7	Pumice LRV 57 в отделке не применён	кофе / табак LRV 8 в отделке не применён	олива LRV 12 в отделке не применён	Bancha LRV 14 текстиль/декор 6	Mouse's Back LRV 26 текстиль/декор 7	Hague Blue — глубокий сине-зелёный LRV 7 акцент 1	Stiffkey Blue — чернильный синий LRV 10.1 акцент 5	Eating Room Red — брусничный красный LRV 11.8 акцент 6	Calke Green — традиционный шалфей LRV 22 акцент 7

План 60/30/10



Окраска, факт — по площади стен, акцентов, потолков

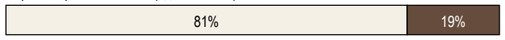

окрашено всего 226,9 м²; второстепенный тон несут мебель и текстиль


Условные обозначения

- **К1** Farrow & Ball No. 2003 · Pointing · Modern Emulsion · матовая · кл. 1
- **К2** Farrow & Ball No. 30 · Hague Blue — глубокий сине-зелёный · Euro Power 7, колеровка по NCS · матовая · кл. 1
- **К3** Tikkurila G503 · Calla · Euro Power 7 · глубокомат. · кл. 2
- **К4** Farrow & Ball No. 2003 · Pointing · МДФ
- **К5** Tikkurila G503 · Calla · Euro Power 7 · матовая · кл. 1
- **К6** Farrow & Ball No. 281 · Stiffkey Blue — чернильный синий · Euro Power 7, колеровка по NCS · матовая · кл. 1
- **К7** Farrow & Ball No. 43 · Eating Room Red — брусничный красный · Modern Emulsion · матовая · кл. 1
- **К8** Farrow & Ball No. 34 · Calke Green — традиционный шалфей · Modern Emulsion · матовая · кл. 1
- дерево (доска, паркет, ламинат) — рисунок досок
- керамогранит, плитка, камень — сетка швов по формату
- **КМ1** аналог: инженерная доска, дуб натуральный, масло, 1-полосная, 14/4 мм
- **КМ2** плитка · аналог: керамогранит под травертин, матовый, 600×1200×9 мм
- **КМ3** аналог: керамогранит ректифицированный под травертин, матовый, 600×600×9 мм
- **КМ4** аналог: керамогранит ректифицированный под травертин, матовый, 600×1200×9 мм
- **КМ5** аналог: керамогранит под травертин, матовый, 1200×600×9 мм

К — краска, КМ — отделочный материал (тон КМ — по описанию, эталон — образец материала); кл. — класс истирания (1 — самый стойкий к мытью); LRV — светлота цвета: 0 — чёрный, 100 — белый

					Проект: Квартира 68 м², элитный модерн			
	Лист	№ док.	Подпись	Дата	Колерная карта	Стадия	Лист	Листов
Дизайнер	Кырлан А.С.			04.11.26		П	11	86

выпуск 04.11.2026 № f0db2de63c · стр. 11 из 86

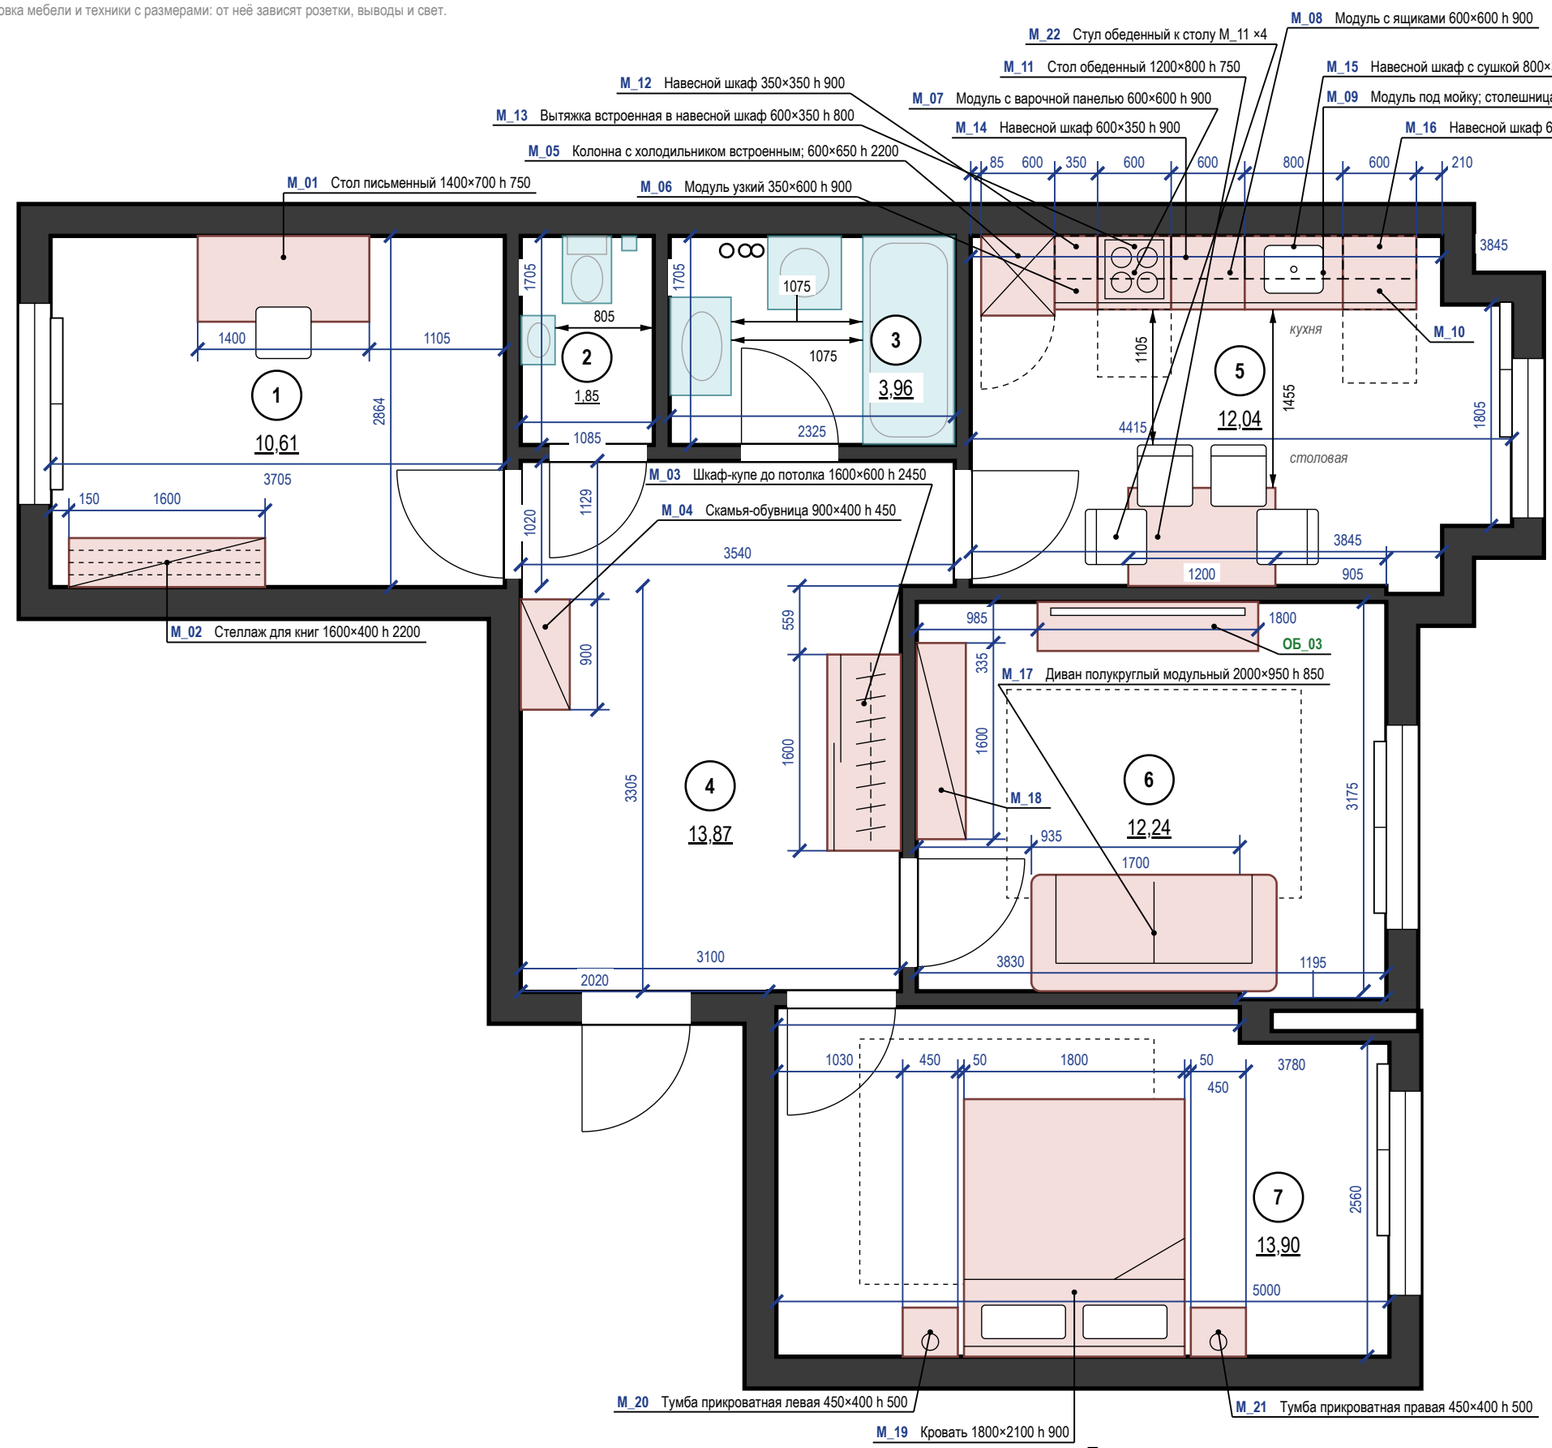

Экспликация помещений

лист 6 · на плане — номера в марках

Ведомость мебели и оборудования

Марка	Наименование	Ш×Г×В, мм	Пом.	Кол.
M_01	Стол письменный 1400×700	1400×700×750	1	1
M_02	Стеллаж для книг 1600×400	1600×400×2200	1	1
M_03	Шкаф-купе 1600×600 до потолка	1600×600×2450	4	1
M_04	Скамья-обувница 900×400	900×400×450	4	1
M_05	Колонна с холодильником встроенным;	600×650×2200	5	1
M_06	Модуль узкий	350×600×900	5	1
M_07	Модуль с варочной панелью	600×600×900	5	1
M_08	Модуль с ящиками	600×600×900	5	1
M_09	Модуль под мойку; столешница	800×600×900	5	1
M_10	Посудомоечная машина встроенная 600	600×600×900	5	1
M_11	Стол обеденный 1200×800	1200×800×750	5	1
M_12	Навесной шкаф	350×350×900	5	1
M_13	Вытяжка встроенная в навесной шкаф	600×350×800	5	1
M_14	Навесной шкаф	600×350×900	5	1
M_15	Навесной шкаф с сушкой	800×350×900	5	1
M_16	Навесной шкаф	600×350×900	5	1
ОБ_03	ТВ-стена в стеновых панелях	1800×400×450	6	1
M_17	Диван полукруглый модульный 2000×950	2000×950×850	6	1
M_18	Консоль 1600×400 красного дерева	1600×400×750	6	1
M_19	Кровать 1800×2100	1800×2100×900	7	1
M_20	Тумба прикроватная левая	450×400×500	7	1
M_21	Тумба прикроватная правая	450×400×500	7	1
M_22	Стул обеденный к столу M_11	450×500×820	5	4

Ш — вдоль стены (изголовья), Г — от стены (длина кровати)

Материалы, модели, допуск замены — лист 13

Примечания

1. Размеры — в мм от чистовых поверхностей стен; размеры мебели уточнить после отделочных работ; общие указания — лист 4.
2. У позиций M_10, ОБ_03, M_18 на плане только марка: наименование и габарит — в спецификации, лист 13.
3. Стулья обеденной группы (M_22 — 4 шт.) показаны в рабочем положении, задвинутыми под столешницу на 150 мм.

					Проект: Квартира 68 м², элитный модерн	M 1:50
	Лист	№ док.	Подпись	Дата		
Дизайнер	Кырлан А.С.			04.11.26	План размещения мебели и оборудования	Стадия: П; Лист: 12; Листов: 86

выпуск 04.11.2026 № f0db2de63c · стр. 12 из 86

Поз.	Наименование и техническая характеристика	Тип, марка, обозначение документа, опросного листа	Код продукции	Поставщик	Ед. измерения	Кол.	Масса 1 ед., кг	Примечание
	Мебель встроенная и корпусная (изготовление по чертежам мебельщика)							
M_03	Шкаф-купе 1600×600 до потолка: филёнчатые фасады эмаль пыльно-синяя и бронзовое зеркало, латунные ручки; корпус ЛДСП 16 мм; фасады — МДФ, шпон / эмаль 18 мм; вставка — зеркало серебро 4 мм на безопасной плёнке, в профиле двери; Ш×Г×В 1600×600×2450 мм			изготовление на заказ	шт.	1		пом. 4
M_05	Колонна с холодильником встроенным; фасады — МДФ: шпон американского ореха (нижние модули) и эмаль пыльно-синяя с узкой филёнкой (колонны), латунные ручки-скобы; фурнитура — латунь брашированная; корпус ЛДСП 16 мм; фасады МДФ: шпон американского ореха (нижние модули) и эмаль пыльно-синяя с узкой филёнкой (колонны), латунные ручки-скобы 18 мм; Ш×Г×В 600×650×2200 мм			изготовление на заказ	шт.	1		пом. 5; крепление к стене
M_06	Модуль узкий с выдвижными ящиками 350; корпус ЛДСП 16 мм; фасады — МДФ: шпон американского ореха (нижние модули) и эмаль пыльно-синяя с узкой филёнкой (колонны), латунные ручки-скобы 18 мм; Ш×Г×В 350×600×900 мм			изготовление на заказ	шт.	1		пом. 5
M_07	Модуль с варочной панелью и духовым шкафом; корпус ЛДСП 16 мм; фасады — МДФ: шпон американского ореха (нижние модули) и эмаль пыльно-синяя с узкой филёнкой (колонны), латунные ручки-скобы 18 мм; Ш×Г×В 600×600×900 мм			изготовление на заказ	шт.	1		пом. 5
M_08	Модуль с ящиками; корпус ЛДСП 16 мм; фасады — МДФ: шпон американского ореха (нижние модули) и эмаль пыльно-синяя с узкой филёнкой (колонны), латунные ручки-скобы 18 мм; Ш×Г×В 600×600×900 мм			изготовление на заказ	шт.	1		пом. 5
M_09	Модуль под мойку; столешница — мрамор с яркой прожилкой (типа Calacatta Viola), 20 мм, фартук одним слэбом; корпус ЛДСП 16 мм; фасады — МДФ: шпон американского ореха (нижние модули) и эмаль пыльно-синяя с узкой филёнкой (колонны), латунные ручки-скобы 18 мм; Ш×Г×В 800×600×900 мм			изготовление на заказ	шт.	1		пом. 5
M_10	Модуль под встраиваемую ПММ 60; без корпуса (ниша между соседними модулями); фасад на дверь машины — МДФ: шпон американского ореха (нижние модули) и эмаль пыльно-синяя с узкой филёнкой (колонны), латунные ручки-скобы 18 мм; цоколь; Ш×Г×В 600×600×900 мм			изготовление на заказ	шт.	1		пом. 5
M_12	Навесной шкаф; корпус ЛДСП 16 мм; фасады — МДФ, эмаль пыльно-синяя, филёнка, латунные ручки 18 мм; Ш×Г×В 350×350×900 мм			изготовление на заказ	шт.	1		пом. 5
M_13	Вытяжка встроенная в навесной шкаф, рециркуляция до обмера вентканала; корпус ЛДСП 16 мм; фасады — МДФ, эмаль пыльно-синяя, филёнка, латунные ручки 18 мм; Ш×Г×В 600×350×800 мм			изготовление на заказ	шт.	1		пом. 5
M_14	Навесной шкаф; корпус ЛДСП 16 мм; фасады — МДФ, эмаль пыльно-синяя, филёнка, латунные ручки 18 мм; Ш×Г×В 600×350×900 мм			изготовление на заказ	шт.	1		пом. 5
M_15	Навесной шкаф с сушкой; корпус ЛДСП 16 мм; фасады — МДФ, эмаль пыльно-синяя, филёнка, латунные ручки 18 мм; Ш×Г×В 800×350×900 мм			изготовление на заказ	шт.	1		пом. 5
M_16	Навесной шкаф; корпус ЛДСП 16 мм; фасады — МДФ, эмаль пыльно-синяя, филёнка, латунные ручки 18 мм; Ш×Г×В 600×350×900 мм			изготовление на заказ	шт.	1		пом. 5
	Мебель покупная							
M_01	Стол письменный 1400×700, шпон ореха на изогнутых опорах, кожаная вставка, латунная фурнитура; дерево — дуб натуральный, металл — чёрный матовый; Ш×Г×В 1400×700×750 мм			аналог по характеристикам	шт.	1		пом. 1; замена ≤ габарита
M_02	Стеллаж для книг 1600×400, каркас — чёрная сталь, полки — дуб натуральный; каркас — чёрная сталь, полки — массив дуб натуральный; Ш×Г×В 1600×400×2200 мм			аналог по характеристикам	шт.	1		пом. 1; крепление к стене; замена ≤ габарита
M_04	Скамья-обувница 900×400, дуб натуральный, с сушилкой для обуви (предложение); дерево — дуб натуральный; Ш×Г×В 900×400×450 мм			аналог по характеристикам	шт.	1		пом. 4; замена ≤ габарита
M_11	Стол обеденный 1200×800 на скульптурной круглой опоре, мрамор с яркой прожилкой; стулья бархат бордо на латунных ножках, 4 шт.; дерево — дуб натуральный; Ш×Г×В 1200×800×750 мм			аналог по характеристикам	шт.	1		пом. 5; замена ≤ габарита
M_22	Стул обеденный к столу M_11; обивка — ткань, цвет Farrow & Ball No. 201; каркас — дуб натуральный; Ш×Г×В 450×500×820 мм			аналог по характеристикам	шт.	4		пом. 5; замена ≤ габарита
M_17	Диван полукруглый модульный 2000×950, глубокая посадка, бархат бордо (оксблад), латунный цоколь; обивка букле; Ш×Г×В 2000×950×850 мм			аналог по характеристикам	шт.	1		пом. 6; замена ≤ габарита

Примечания

1. Позиции мебели совпадают с марками на плане расстановки; размеры Ш×Г×В — Ш вдоль стены, Г от стены.
2. Размеры и привязки плана расстановки — в мм от чистовых поверхностей стен: слой штукатурки 20 мм по блоку и 5 мм шпаклёвки по ГКЛ учтён; привязки — от стен и углов помещения, а не от другой мебели.
3. План расстановки не является документацией для изготовления мебели. Встроенная и корпусная мебель изготавливается по чертежам мебельщика после контрольного обмера (после штукатурки); «стена в стену» — с зазором 10 мм с каждой стороны или с компенсаторами; графы «Тип, марка» и «Код продукции» для неё не заполняются (ГОСТ 21.110-2013).
4. Покупные изделия — аналог по характеристикам: заменять только на изделия не больше указанного габарита и того же материала и цвета.
5. Материал и цвет, не указанные в данных изделия, приняты по концепции: тон дерева — по полу, обивка — по вторичному цвету палитры; образцы согласовать до заказа.
6. Масса 1 ед. для изделий до 25 кг не указывается. Техника — по монтажным схемам изготовителя; выводы — по листам ЭОМ и ВК.

					Проект: Квартира 68 м², элитный модерн
	Лист	№ док.	Подпись	Дата	
Дизайнер	Кырлан А.С.			04.11.26	Спецификация мебели и оборудования

Стадия	Лист	Листов
П	13	86

Поз.	Наименование и техническая характеристика	Тип, марка, обозначение документа, опросного листа	Код продукции	Поставщик	Ед. измерения	Кол.	Масса 1 ед., кг	Примечание
M_18	Консоль 1600×400 красного дерева (шпон сапеле) на гнутых ножках, мраморная столешница с яркой прожилкой; пуф бархат; дерево — дуб натуральный; Ш×Г×В 1600×400×750 мм			аналог по характеристикам	шт.	1		пом. 6; крепление к стене; замена ≤ габарита
ОБ_03	ТВ-стена в стеновых панелях с молдингами и арочной нишей с подсветкой; тумба 1800×400 шпон ореха, мраморная столешница, ТВ 55" дерево — дуб натуральный; Ш×Г×В 1800×400×450 мм			аналог по характеристикам	шт.	1		пом. 6; замена ≤ габарита
M_19	Кровать 1800×2100 с панельным изголовьем во всю стену: стёганый бархат шалфей, латунный кант; обивка кожа натуральная, дерево — дуб натуральный; Ш×Г×В 1800×2100×900 мм			аналог по характеристикам	шт.	1		пом. 7; замена ≤ габарита
M_20	Тумба прикроватная левая, дуб натуральный; дерево — дуб натуральный; Ш×Г×В 450×400×500 мм			аналог по характеристикам	шт.	1		пом. 7; замена ≤ габарита
M_21	Тумба прикроватная правая, дуб натуральный; дерево — дуб натуральный; Ш×Г×В 450×400×500 мм			аналог по характеристикам	шт.	1		пом. 7; замена ≤ габарита
	Техника встраиваемая и бытовая (покупные изделия), светильники под розетки							
	Стиральная машина, место по листу ВК (ОБ_01); Ш×Г 600×600 мм	аналог по характеристикам: фронтальная загрузка, в плане 600 × 600 мм (ширина × глубина), по листу ВК		по выбору заказчика до изготовления мебели	шт.	1		пом. 3; по схеме изготовителя
	Сушильная машина встраиваемая, у M_04	аналог по характеристикам: тип загрузки — по листу ВК, по листу ВК		по выбору заказчика до изготовления мебели	шт.	1		пом. 4; по схеме изготовителя
	Холодильник встраиваемый, в модуле M_05	аналог по характеристикам: полновстраиваемый под фасад, ниша 1780 × 560 × 550 мм, вентиляция решётка в цоколе, выход сверху		по выбору заказчика до изготовления мебели	шт.	1		пом. 5; по схеме изготовителя
	Духовой шкаф встраиваемый, в модуле M_07	аналог по характеристикам: 60 см, лицевая панель 595 мм, ниша 560 × 600, глубина ≥ 550 мм, вентиляция за прибором		по выбору заказчика до изготовления мебели	шт.	1		пом. 5; по схеме изготовителя
	Варочная панель встраиваемая, индукционная, в модуле M_07	аналог по характеристикам: индукционная 60 см, вырез 560 × 490 мм по шаблону модели		по выбору заказчика до изготовления мебели	шт.	1		пом. 5; по схеме изготовителя
	Посудомоечная машина встраиваемая, в модуле M_10; ниша 600 мм	аналог по характеристикам: полновстраиваемая 60 см под фасад, ниша 600 × 862 мм, навеска фасада в комплекте		по выбору заказчика до изготовления мебели	шт.	1		пом. 5; по схеме изготовителя
	Вытяжка встраиваемая, в модуле M_13	аналог по характеристикам: производительность — по расчёту ОВ, шум ≤ 55 дБ(А)		по выбору заказчика до изготовления мебели	шт.	1		пом. 5; по схеме изготовителя
	Торшер, у поз. M_17; абажур — ткань или опаловое стекло; лампа 2700 K			аналог по характеристикам	шт.	1		пом. 6; розетка Р13 (ЭОМ)
	Торшер, у поз. M_17; абажур — ткань или опаловое стекло; лампа 2700 K			аналог по характеристикам	шт.	1		пом. 6; розетка Р36 (ЭОМ)
	Торшер, у поз. M_17; абажур — ткань или опаловое стекло; лампа 2700 K			аналог по характеристикам	шт.	1		пом. 6; розетка Р37 (ЭОМ)
	Текстиль							
T1	Портьеры в пол на потолочном карнизе, бархат (тон по комнате); лён / хлопок / шерсть по ткани, подкладка полиэстер; цвет Farrow & Ball No. 201; карниз 2040 мм, высота 2575 мм, сборка 2			аналог по характеристикам	шт.	2		пом. 1
T2	Тюль лён натуральный в пол; лён / хлопок / полиэстер по ткани; цвет Tikkurila G503; карниз 2040 мм, высота 2575 мм, сборка 2,5			аналог по характеристикам	шт.	1		пом. 1
T3	Рулонная штора в проёме окна, ткань блэкаут; полиэстер 100 %; цвет Farrow & Ball No. 201; карниз 1260 мм, высота 1460 мм			аналог по характеристикам	шт.	1		пом. 5
T4	Портьеры в пол на потолочном карнизе, бархат (тон по комнате); лён / хлопок / шерсть по ткани, подкладка полиэстер; цвет Farrow & Ball No. 201; карниз 2065 мм, высота 2575 мм, сборка 2			аналог по характеристикам	шт.	2		пом. 6
T5	Тюль лён натуральный в пол; лён / хлопок / полиэстер по ткани; цвет Tikkurila G503; карниз 2065 мм, высота 2575 мм, сборка 2,5			аналог по характеристикам	шт.	1		пом. 6

					Проект: Квартира 68 м², элитный модерн	
	Лист	№ док.	Подпись	Дата	Спецификация мебели и оборудования (продолжение)	Стадия: П; Лист: 14; Листов: 86
Дизайнер	Кырлан А.С.			04.11.26		

Поз.	Наименование и техническая характеристика	Тип, марка, обозначение документа, опросного листа	Код продукции	Поставщик	Ед. измерения	Кол.	Масса 1 ед., кг	Примечание
Т6	Ковёр фактурный шерсть с джутом, тёплый терракотовый тон; шерсть / джут / хлопок по ткани; цвет Farrow & Ball No. 201; 2400×1700 мм			аналог по характеристикам	шт.	1		пом. 6; с подложкой
Т7	Подушки бархат и жаккард: бордо, шалфей, горчица; натуральное волокно по ткани; цвет NCS S 2010-Y30R			аналог по характеристикам	шт.	3		пом. 6
Т8	Подушки бархат и жаккард: бордо, шалфей, горчица; натуральное волокно по ткани; цвет Farrow & Ball No. 298			аналог по характеристикам	шт.	2		пом. 6
Т9	Плед шерсть с бахромой, терракота; шерсть / хлопок по ткани; цвет Farrow & Ball No. 298			аналог по характеристикам	шт.	1		пом. 6
Т10	Портьеры в пол на потолочном карнизе, бархат (тон по комнате); лён / хлопок / шерсть по ткани, подкладка полиэстер; цвет Farrow & Ball No. 201; карниз 2265 мм, высота 2635 мм, сборка 2			аналог по характеристикам	шт.	2		пом. 7
Т11	Тюль лён натуральный в пол; лён / хлопок / полиэстер по ткани; цвет Tikkurila G503; карниз 2265 мм, высота 2635 мм, сборка 2,5			аналог по характеристикам	шт.	1		пом. 7
Т12	Ковёр фактурный шерсть с джутом, тёплый терракотовый тон; шерсть / джут / хлопок по ткани; цвет Farrow & Ball No. 201; 2400×2000 мм			аналог по характеристикам	шт.	1		пом. 7; с подложкой
Т13	Подушки бархат и жаккард: бордо, шалфей, горчица; натуральное волокно по ткани; цвет NCS S 2010-Y30R			аналог по характеристикам	шт.	3		пом. 7
Т14	Подушки бархат и жаккард: бордо, шалфей, горчица; натуральное волокно по ткани; цвет Farrow & Ball No. 40			аналог по характеристикам	шт.	2		пом. 7
Т15	Плед шерсть с бахромой, терракота; шерсть / хлопок по ткани; цвет Farrow & Ball No. 40			аналог по характеристикам	шт.	1		пом. 7
	Декор							
ДК9	Зеркало над умывальником, влагостойкое, с подсветкой; 400×800 мм; низ на 1200 мм от пола			аналог по характеристикам	шт.	1	5	пом. 2; крепление к стене
ДК10	Зеркало над умывальником, влагостойкое, с подсветкой; 600×800 мм; низ на 1200 мм от пола			аналог по характеристикам	шт.	1	5	пом. 3; крепление к стене
ДК1	Зеркало над скамьёй 600×1200, тонкая чёрная рама; 600×1200 мм; низ на 700 мм от пола			аналог по характеристикам	шт.	1	6	пом. 4; крепление: дюбель 2 шт.
ДК2	Ваза с живыми цветами на обеденном столе; 200×300 мм; на M_11			аналог по характеристикам	шт.	1		пом. 5
ДК3	Часы настенные Ø300; 300×300 мм; низ на 1700 мм от пола			аналог по характеристикам	шт.	1	1	пом. 5; крепление к стене
ДК4	Крупная живопись в тонкой латунной раме над консоль низкая 1600×400: крупная абстракция широкими мазками, рама дуб натуральный; 1050×750 мм; низ на 1000 мм от пола			аналог по характеристикам	шт.	1	4	пом. 6; крепление к стене
ДК5	Крупная живопись в тонкой латунной раме над диван 2000×950: чёрно-белая фотография города в дожде, рама — дуб натуральный; 1200×850 мм; низ на 1050 мм от пола			аналог по характеристикам	шт.	1	4	пом. 6; крепление к стене
ДК6	Оливковое дерево в кашпо Ø450; 450×450 мм			аналог по характеристикам	шт.	1		пом. 6
ДК7	Крупная живопись в тонкой латунной раме над кровать 1400×2000: пересекающиеся дуги, рама — дуб натуральный; 900×650 мм; низ на 1100 мм от пола			аналог по характеристикам	шт.	1	4	пом. 7; крепление к стене
ДК8	Монстера в кашпо Ø450; 450×450 мм			аналог по характеристикам	шт.	1		пом. 7

					Проект: Квартира 68 м², элитный модерн
	Лист	№ док.	Подпись	Дата	
Дизайнер	Кырлан А.С.			04.11.26	Спецификация мебели и оборудования (продолжение)

Стадия	Лист	Листов
П	15	86

Правка к этому листу

Ведомость изделий

Марка	Наименование	Пом.	Ш×Г×В, мм	Корпус	Фасад	Кромка, мм	Кол.
M_03	Шкаф-купе	4	1600×600×2450	ЛДСП 16	МДФ, шпон / эмаль 18 мм; вставка зеркало серебро 4 мм на безопасной плёнке, в профиле двери	0,4 / 1	1
M_05	Пенал: холодильник встр.	5	600×650×2200	ЛДСП 16	МДФ: шпон американского ореха (нижние модули) и эмаль пыльно-синяя с узкой филёнкой (колонны), латунные ручки-скобы 18 мм	0,4 / 1	1
M_06	Модуль нижний: ящики	5	350×600×900	ЛДСП 16	МДФ: шпон американского ореха (нижние модули) и эмаль пыльно-синяя с узкой филёнкой (колонны), латунные ручки-скобы 18 мм	0,4 / 1	1
M_12	Модуль навесной: полки	5	350×350×900	ЛДСП 16	МДФ, эмаль пыльно-синяя, филёнка, латунные ручки 18 мм	0,4 / 1	1
M_07	Модуль нижний: духовой шкаф, варочная	5	600×600×900	ЛДСП 16	МДФ: шпон американского ореха (нижние модули) и эмаль пыльно-синяя с узкой филёнкой (колонны), латунные ручки-скобы 18 мм	0,4 / 1	1
M_13	Модуль навесной: полки	5	600×350×800	ЛДСП 16	МДФ, эмаль пыльно-синяя, филёнка, латунные ручки 18 мм	0,4 / 1	1
M_08	Модуль нижний: ящики	5	600×600×900	ЛДСП 16	МДФ: шпон американского ореха (нижние модули) и эмаль пыльно-синяя с узкой филёнкой (колонны), латунные ручки-скобы 18 мм	0,4 / 1	1
M_14	Модуль навесной: полки	5	600×350×900	ЛДСП 16	МДФ, эмаль пыльно-синяя, филёнка, латунные ручки 18 мм	0,4 / 1	1
M_09	Модуль нижний: мойка	5	800×600×900	ЛДСП 16	МДФ: шпон американского ореха (нижние модули) и эмаль пыльно-синяя с узкой филёнкой (колонны), латунные ручки-скобы 18 мм	0,4 / 1	1
M_15	Модуль навесной: сушка	5	800×350×900	ЛДСП 16	МДФ, эмаль пыльно-синяя, филёнка, латунные ручки 18 мм	0,4 / 1	1
M_10	Модуль под ПММ 60: без корпуса, фасад на дверь машины	5	600×600×900	без корпуса	МДФ: шпон американского ореха (нижние модули) и эмаль пыльно-синяя с узкой филёнкой (колонны), латунные ручки-скобы 18 мм — на дверь машины (навеска из её комплекта), цоколь		1
M_16	Модуль навесной: полки	5	600×350×900	ЛДСП 16	МДФ, эмаль пыльно-синяя, филёнка, латунные ручки 18 мм	0,4 / 1	1

Ведомость встраиваемой техники

Поз.	Прибор	Ниша, вырез, мм	Вентиляция	Питание	Схема
M_05	Холодильник встраиваемый, ниша 1780	ниша 1780 × 560 × 550	решётка в цоколе, канал за корпусом, выход сверху	Р7: M_05, H=2050 — над нишей холодильника, съёмная панель	по модели
M_07	Духовой шкаф встраиваемый, 60 см	ниша 560 × 600, глубина ≥ 550	зазор за шкафом, вырез в задней стенке	ЭВ2: M_07, H=150 — под духовым шкафом, доступ через ящик	по модели
M_07	Варочная панель индукционная, 60 см	вырез в столешнице 560 × 490		ЭВ1: M_06, H=600 — в соседнем модуле, за ящиком	по модели
M_09	Мойка врезная / подстольная с сифоном	вырез по шаблону, ориентир 700 × 480		смеситель — выводы ВК	по модели
M_10	Посудомоечная машина встраиваемая, 60 см	ниша 600 × 862 (от пола до низа столешницы)	зазор в цоколе, по схеме	Р6: M_10, H=300 — за ПММ — перенести в соседний модуль	по модели
M_13	Вытяжка встраиваемая в навесной модуль, 60 см	низ ≥ 650 над панелью	воздуховод к вентканалу, короб до потолка	ЭВ3: M_13, H=2200 — в навесном модуле	по модели

Ведомость фурнитуры

№	Фурнитура	Тип, размер	Изделия	Кол.
1	Система дверей купе: профиль, направляющие, ролики	на 2 двери	M_03	1
2	Ручка-профиль вертикальная	в цвет профиля	M_03	2
3	Полкодержатель с фиксацией	ø5 мм	M_03, M_05, M_12, M_13, M_14, M_16	40
4	Штанга овальная 30×15, L = 776	+ 2 держателя	M_03	1
5	Полка для обуви выдвижная наклонная	ширина 776	M_03	3
6	Опора регулируемая с цоколем на клипсах	ход 20 мм	M_03	6
7	Анкер по основанию стены	по таблице крепежа	M_03, M_12, M_13, M_14, M_15, M_16	15
8	Уголок крепления к стене от опрокидывания	стальной	M_03, M_05	4
9	Петля накладная 110° с доводчиком	чашка 35 мм	M_05, M_12, M_13, M_14, M_09, M_15, M_16	29
10	Ручка-профиль	латунь матовая	M_05, M_06, M_12, M_07, M_13, M_08, M_14, M_09, M_15, M_10, M_16	22
11	Опора кухонная регулируемая 100–120 мм	+ клипса цоколя	M_05, M_06, M_07, M_08, M_09	22
12	Направляющие полного выдвижения с доводчиком NL 500	пара	M_06, M_07, M_08	7
13	Навес регулируемый для навесного шкафа	пара на секцию	M_12, M_13, M_14, M_15, M_16	5
14	Шина монтажная	L = 290	M_12	1
15	Шина монтажная	L = 540	M_13, M_14, M_16	3
16	Сушка для посуды в шкаф	ширина 800	M_15	1
17	Шина монтажная	L = 740	M_15	1
18	Комплект навески фасада ПММ	из поставки машины	M_10	1

Примечания


1. Модели техники выбирает заказчик до изготовления мебели; ниши, вырезы и вентиляция — по монтажной схеме выбранной модели (условие гарантии), её номер вносится в ведомость.
2. Количество фурнитуры — по чертежам изделий; запас крепежа 5 %. Аналоги — по характеристикам (доводчик, нагрузка, ход).
3. Цвет корпусов, фасадов и профилей — по колерной карте проекта. Кромка — скрытые / видимые торцы, мм.

					Проект: Квартира 68 м², элитный модерн
	Лист	№ док.	Подпись	Дата	Ведомости изделий, техники и фурнитуры
Дизайнер	Кырлан А.С.			04.11.26	


Стадия	Лист	Листов
П	16	86

выпуск 04.11.2026 № f0db2de63c · стр. 16 из 86


Фрагмент 1. Санузел (пом. 2)

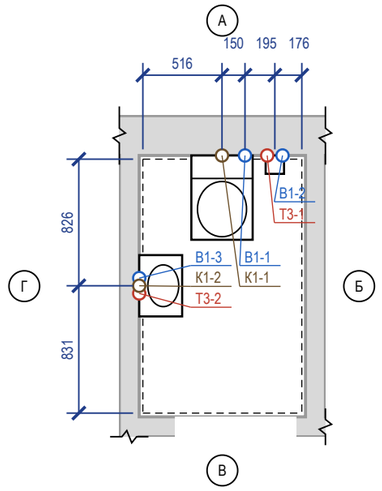

Фрагмент 2. Ванная (пом. 3)

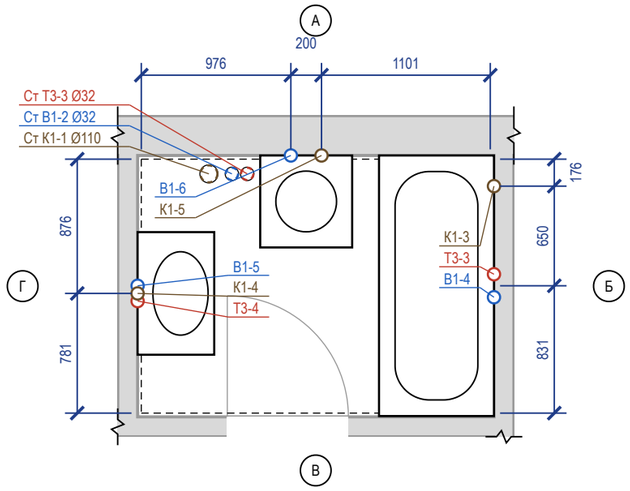

Фрагмент 3. Кухня-столовая (пом. 5)

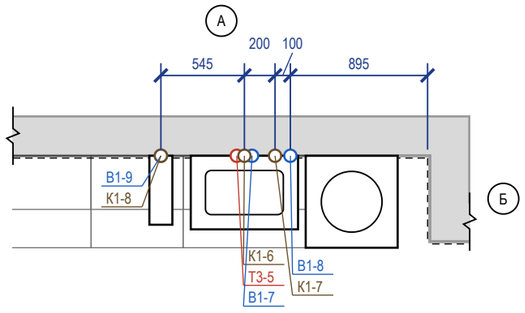

Ведомость привязок выводов

Код	Прибор	Ø	H, мм	Привязка от чист. стен, мм	Прим.
В1-1	С_01 унитаз подвесной	½"	1000	ст. А: 371 от Б	в раме инсталляции
К1-1	С_01 унитаз подвесной	Ø110	220	ст. А: 516 от Г	
В1-2	С_02 гигиенический душ	½"	750	ст. А: 126 от Б	межос. 100
Т3-1	С_02 гигиенический душ	½"	750	ст. А: 226 от Б	межос. 100
В1-3	С_03 умывальник	½"	550	ст. Г: 776 от А	межос. 100
Т3-2	С_03 умывальник	½"	550	ст. Г: 781 от В	межос. 100
К1-2	С_03 умывальник	Ø40	500	ст. Г: 826 от А	
В1-4	С_04 ванна	½"	800	ст. Б: 756 от В	межос. 150
Т3-3	С_04 ванна	½"	800	ст. Б: 751 от А	межос. 150
К1-3	С_04 ванна	Ø50	50	ст. Б: 176 от А	
В1-5	С_05 умывальник	½"	550	ст. Г: 826 от А	межос. 100
Т3-4	С_05 умывальник	½"	550	ст. Г: 731 от В	межос. 100
К1-4	С_05 умывальник	Ø40	500	ст. Г: 781 от В	
В1-6	ОБ_01 стиральная машина	½"	600	ст. А: 976 от Г	кран машины
К1-5	ОБ_01 стиральная машина	Ø40	600	ст. А: 1101 от Б	
В1-7	С_06 мойка кухонная	½"	600	ст. А: 1145 от Б	межос. 100
Т3-5	С_06 мойка кухонная	½"	600	ст. А: 1245 от Б	межос. 100
К1-6	С_06 мойка кухонная	Ø50	400	ст. А: 1195 от Б	
В1-8	ОБ_02 посудомоечная машина	½"	550	ст. А: 895 от Б	кран ПММ в шкафу мойки
К1-7	ОБ_02 посудомоечная машина	Ø40	550	ст. А: 995 от Б	слив ПММ в шкафу мойки
В1-9	С_07 фильтр обратного осмоса	½"	550	ст. А: 1740 от Б	
К1-8	С_07 фильтр обратного осмоса	Ø40	450	ст. А: 1740 от Б	

Условные обозначения


- вывод В1 (код — в ведомости привязок)
- вывод Т3 (код — в ведомости привязок)
- вывод К1 (код — в ведомости привязок)
- сантехприбор по расстановке (габарит модели)
- чистовая поверхность стены (от неё привязки)
- стояк «Ст К1-N / Ст В1-N» (ГОСТ 21.601), Ø мм
- стояк Т3 не на обмере — принят в шахте рядом со Ст В1, сверить
- линия обрыва (граница фрагмента)
- А — обозначение стены А–Г (как на развёртках)

Примечания


1. Привязки выводов даны от чистовых поверхностей стен (облицовка на сторону: санузел — 24 мм (штукатурка 10 + клей 5 + плитка 9); ванная — 24 мм (штукатурка 10 + клей 5 + плитка 9); кухня-столовая — 24 мм (фартук: штукатурка 10 + клей 5 + плитка 9)); эти же грани — на развёртках и в раскладке плитки. Высоты — от чистого пола помещения.
2. До черновой разводки сверить по паспорту выбранного прибора (смеситель, инсталляция, сифон).
3. Горячая вода (Т3) — слева от холодной (В1), если смотреть на прибор. Допуск установки выводов: ±5 мм в группе, ±20 мм у отдельно стоящих.
4. Расчёт систем водоснабжения и канализации и подбор оборудования выполняет проектная организация; лист задаёт места и высоты выводов.
5. Посудомоечная машина ОБ_02: кран и слив — отдельными выводами в шкафу мойки (не за машиной), до машины ≤ 1500 мм.
6. Ст К1-1, Ст В1-2, Ст Т3-3 на обмере не показаны: положение принято (исполнитель по плану заказчика), не замерено; положение сверить на объекте до разметки.
7. Стояки в коробах/шахтах не замоноличивать; стояк К1 в коробе — звукоизоляция стояка в коробе без жёсткого контакта с трубой; к арматуре и ревизиям — люк не меньше 300×400.

					Проект: Квартира 68 м², элитный модерн — М 1:40
	Лист	№ док.	Подпись	Дата	
Дизайнер	Кырлан А.С.			04.11.26	План выводов сантехники
					Стадия: П; Лист: 17; Листов: 86


План квартиры (М 1:200)

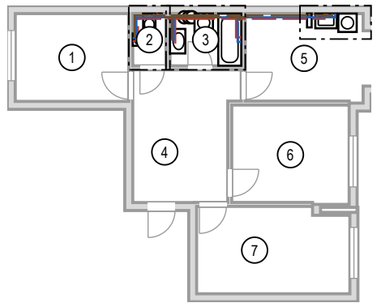


Фр. 3. Кухня-столовая (М 1:25)

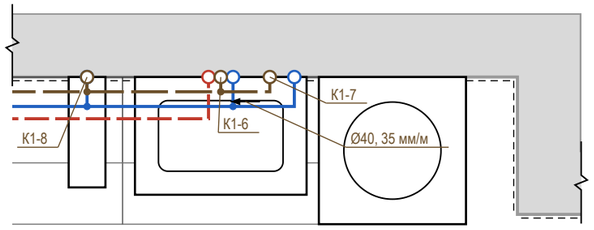

Фр. 1. Санузел (М 1:25)

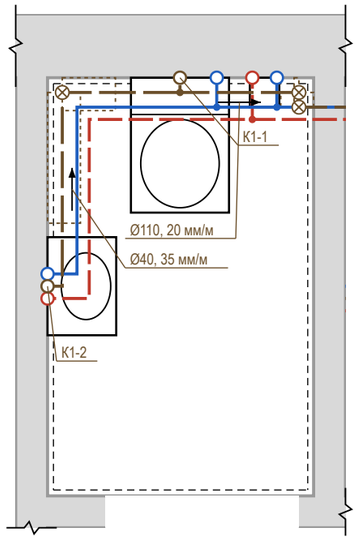

Фр. 2. Ванная (М 1:25)

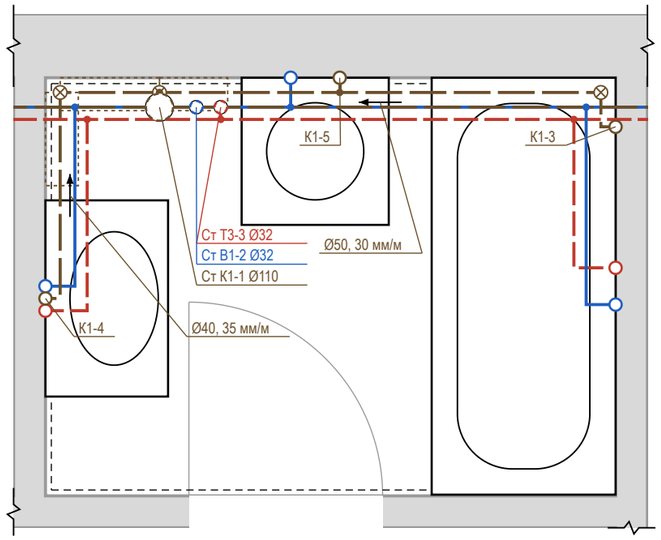

Условные обозначения


- В1 — водопровод хозяйственно-питьевой (ХВС), PP-R Ø20
- Т3 — горячее водоснабжение, подача (ГВС), PP-R Ø20
- К1 — канализация бытовая
- направление уклона К1 / пола: Ø, мм на 1 м
- ревизия (прочистка) К1 — доступ сохранить
- тройник (ответвление к прибору)
- короб К1 над чистым полом (ГКЛВ под плитку)
- вывод В1 (код — в ведомости привязок)
- вывод Т3 (код — в ведомости привязок)
- вывод К1 (код — в ведомости привязок)
- сантехприбор по расстановке (габарит модели)
- стояк «Ст К1-N / Ст В1-N» (ГОСТ 21.601), Ø мм
- стояк Т3 не на обмере — принят в шахте рядом со Ст В1, сверить
- линия обрыва (граница фрагмента)
- граница фрагмента на плане (Фр. N)

Профиль выпусков К1 (до врезки в стояк)

Выпуск	Прибор	Ø	L, м	i, мм/м	Δh, мм	Прокладка, мм
К1-1	С_01 унитаз подвесной	Ø110	1,26	20	25	в полу не помещается: 210 > 90; до решения
К1-6	С_06 мойка кухонная	Ø50	4,75	30	142	над полом за приборами
К1-3	С_04 ванна	Ø50	2,06	30	62	в полу не помещается: 187 > 90; до решения
К1-7	ОБ_02 посудомоечная машина	Ø40	4,95	35	173	над полом за приборами
К1-8	С_07 фильтр обратного осмоса	Ø40	4,20	35	147	над полом за приборами
К1-2	С_03 умывальник	Ø40	2,53	35	89	короб 160×110
К1-4	С_05 умывальник	Ø40	1,36	35	48	короб 120×110
К1-5	ОБ_01 стиральная машина	Ø40	0,85	35	30	короб 100×110

Короб h×b: h — от чистого пола, b — от чистовой стены. Стяжка 90 мм — лист полов.

Узел ввода В1, Т3 (по данным, без масштаба)

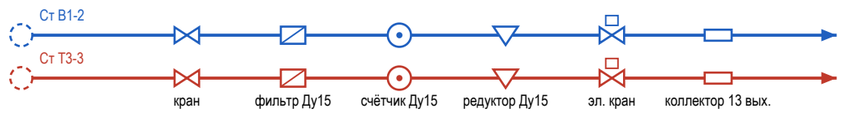

⊗ Ст К1-1: ревизия на стояке — люк в коробе

Примечания

1. Трассы принципиальные, построены от стояков вдоль стен помещений; фактическое положение фиксируется исполнительной схемой с привязками (фото с рулеткой) до закрытия.
2. Уклон К1 не менее 1/d и не более 150 мм/м (СП 30.13330.2020, п. 19.1), приняты практические уклоны; поворот — двумя отводами 45°, ревизия после поворота, доступ сохранить. Стояк К1 в коробе — звукоизоляция стояка в коробе, без жёсткого контакта короба с трубой.
3. Решение по К1: стяжка 90 мм не укрывает трубы (нужно Ø + Δh + 45 мм) — выпуски идут над чистым полом вдоль стен: К1-6, К1-7, К1-8 — за приборами и в раме инсталляции; К1-2, К1-4, К1-5 — в коробе ГКЛВ под плитку (размеры в профиле). Короба — на развёртках; отметку низа врезки в стояк замерить до черновых работ.
4. К1-1 (С_01 унитаз подвесной): Δh 25 + Ø110 + 45 = 210 мм > пирога 90 мм — в стяжке не помещается: подиум или подъём пола на 120 мм, короб 170×140 или прибор ближе к стояку — решение заказчика; до решения не выполнять.
5. К1-3 (С_04 ванна): Δh 62 + Ø50 + 45 = 187 мм > пирога 90 мм — в стяжке не помещается: подиум или подъём пола на 100 мм, короб 150×110 или прибор ближе к стояку — решение заказчика; до решения не выполнять.
6. Отводы К1-6 (4,7 м), К1-7 (4,9 м), К1-8 (4,2 м) длиннее 4 м без вентиляции — у прибора воздушный клапан Ø50 в доступном месте (за люком или в тумбе) либо вентилируемый отвод (EN 12056-2, табл. 4), подбор — проектная организация.
7. Узел ввода В1, Т3 — по данным проекта: кран → фильтр Ду15 → счётчик Ду15 → редуктор Ду15 → эл. кран → коллектор 13 вых.. Доступ к арматуре — через люк не меньше 300×400. Водопровод — в штробе стен или в коробах; трубы испытать давлением до закрытия (акт скрытых работ).
8. Расчёт систем, диаметры магистралей и подбор оборудования выполняет проектная организация; врезка и перенос стояков — по согласованию с управляющей организацией. Арматуру и привязки сверить по паспортам приборов.
9. Ст К1-1, Ст В1-2, Ст Т3-3 на обмере не показаны: положение принято (исполнитель по плану заказчика), не замерено; положение сверить на объекте до разводки.


					Проект: Квартира 68 м², элитный модерн
	Лист	№ док.	Подпись	Дата	
Дизайнер	Кырлан А.С.			04.11.26	Схема разводки водопровода и канализации

Стадия	Лист	Листов
П	18	86

выпуск 04.11.2026 № f0db2de63c · стр. 18 из 86

Правка к этому листу

Схема В1 (М 1:50; по вертикали и горизонтали один масштаб, глубина — ×0,5 под 45°)

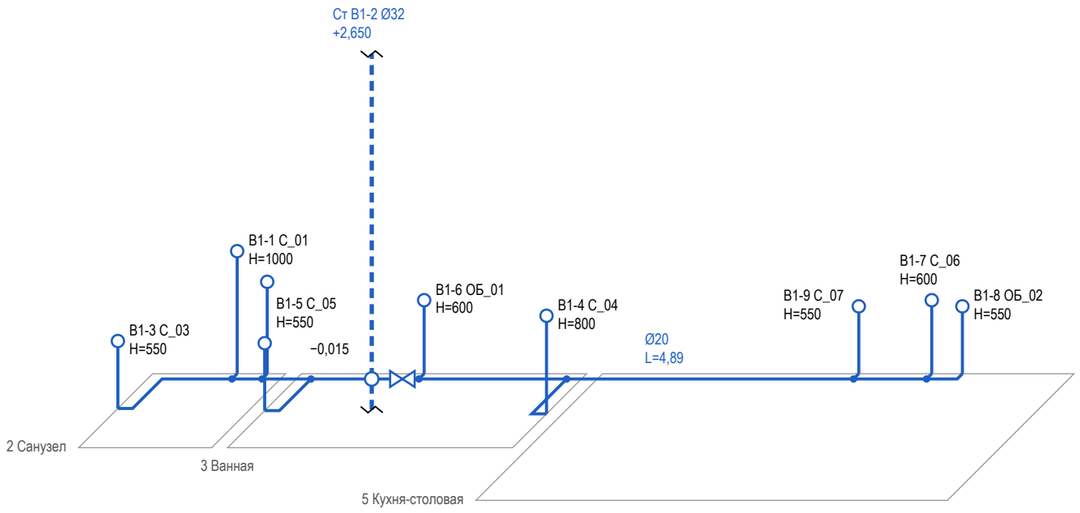

Условные обозначения

- В1 — водопровод хозяйственно-питьевой (ХВС), PP-R Ø20
- вывод В1 (код — в ведомости привязок)
- стояк «Ст К1-N / Ст В1-N» (ГОСТ 21.601), Ø мм
- стояк в плане (на отметке пола); вертикаль — стояк по высоте, разрыв — перекрытие
- тройник (ответвление к прибору)
- кран шаровой
- стояк Т3 не на обмере — принят в шахте рядом со Ст В1, сверить


Примечания

1. Схема В1 построена по тем же трассам, что план разводки: положение в плане сохранено, глубина — в масштабе ×0,5. Трассы принципиальные; фактическое положение фиксируется исполнительной схемой до закрытия.
2. Высоты Н — от чистого пола помещения, мм. Прокладка магистрали В1 по данным: коллекторная разводка, в стяжке пола, в стяжке пола, выше плиты перекрытия; отметка трасс — по пирогу пола.
3. Узел ввода В1 (кран, фильтр, счётчик, обратный клапан, кран) — на схеме разводки; состав узла ввода — по согласованию. Кран шаровой — на первом участке от стояка.
4. Ст В1-2 на обмере не показаны: положение принято (исполнитель по плану заказчика), не замерено; положение сверить на объекте до разводки.
5. Трубы испытать давлением до закрытия (акт скрытых работ, опрессовка по СП 73.13330.2016).
6. Диаметры, высоты выводов и места кранов — по паспортам выбранных приборов и расчёту проектной организации.
7. Расчёт систем, диаметры магистралей и подбор оборудования выполняет проектная организация.

					Проект: Квартира 68 м², элитный модерн	М 1:50
	Лист	№ док.	Подпись	Дата		
Дизайнер	Кырлан А.С.			04.11.26	Аксонометрическая схема В1 (холодное водоснабжение)	Стадия: П; Лист: 19; Листов: 86

Правка к этому листу

Схема Т3 (М 1:50; по вертикали и горизонтали один масштаб, глубина — ×0,5 под 45°)

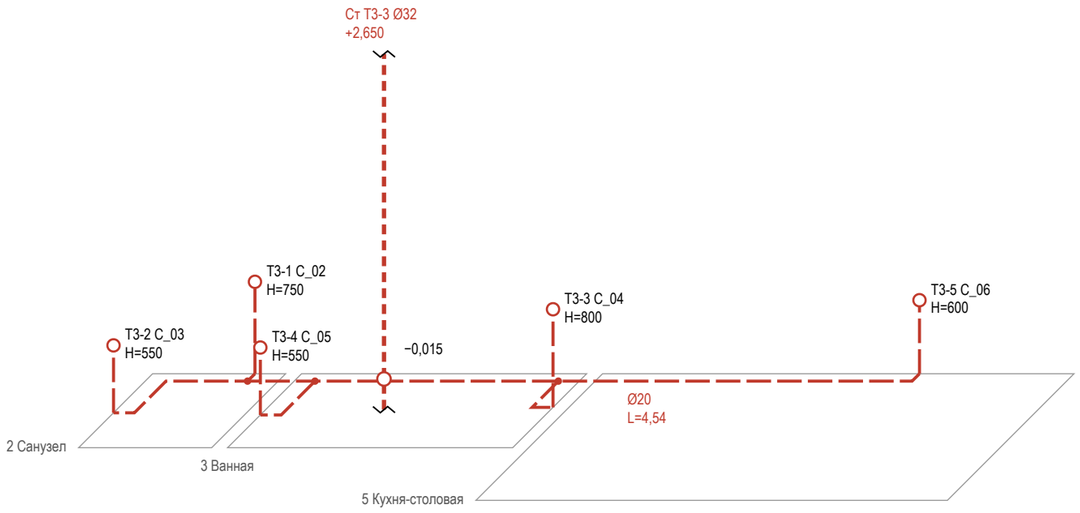

Условные обозначения

- Т3 — горячее водоснабжение, подача (ГВС), PP-R Ø20
- вывод Т3 (код — в ведомости привязок)
- стояк «Ст К1-N / Ст В1-N» (ГОСТ 21.601), Ø мм
- стояк в плане (на отметке пола); вертикаль — стояк по высоте, разрыв — перекрытие
- тройник (ответвление к прибору)
- кран шаровой
- стояк Т3 не на обмере — принят в шахте рядом со Ст В1, сверить

Примечания


1. Схема Т3 построена по тем же трассам, что план разводки: положение в плане сохранено, глубина — в масштабе ×0,5. Трассы принципиальные; фактическое положение фиксируется исполнительной схемой до закрытия.
2. Высоты Н — от чистого пола помещения, мм. Прокладка магистрали Т3 по данным: коллекторная разводка, в стяжке пола, в стяжке пола, выше плиты перекрытия; отметка трасс — по пирогу пола.
3. Узел ввода Т3 (кран, фильтр, счётчик, обратный клапан, кран) — на схеме разводки; состав узла ввода — по согласованию. Кран шаровой — на первом участке от стояка.
4. Циркуляция ГВС в данных не задана — циркуляционного трубопровода на схеме нет.
5. Ст Т3-3 на обмере не показаны: положение принято (исполнитель по плану заказчика), не замерено; положение сверить на объекте до разводки.
6. Трубы испытать давлением до закрытия (акт скрытых работ, опрессовка по СП 73.13330.2016).
7. Диаметры, высоты выводов и места кранов — по паспортам выбранных приборов и расчёту проектной организации.
8. Расчёт систем, диаметры магистралей и подбор оборудования выполняет проектная организация.

					Проект: Квартира 68 м², элитный модерн	М 1:50
	Лист	№ док.	Подпись	Дата		
Дизайнер	Кырлан А.С.			04.11.26	Аксонометрическая схема Т3 (горячее водоснабжение)	Стадия: П; Лист: 20; Листов: 86

выпуск 04.11.2026 № f0db2de63c · стр. 20 из 86

Правка к этому листу

Схема К1 (М 1:50; по вертикали и горизонтали один масштаб, глубина — ×0,5 под 45°)

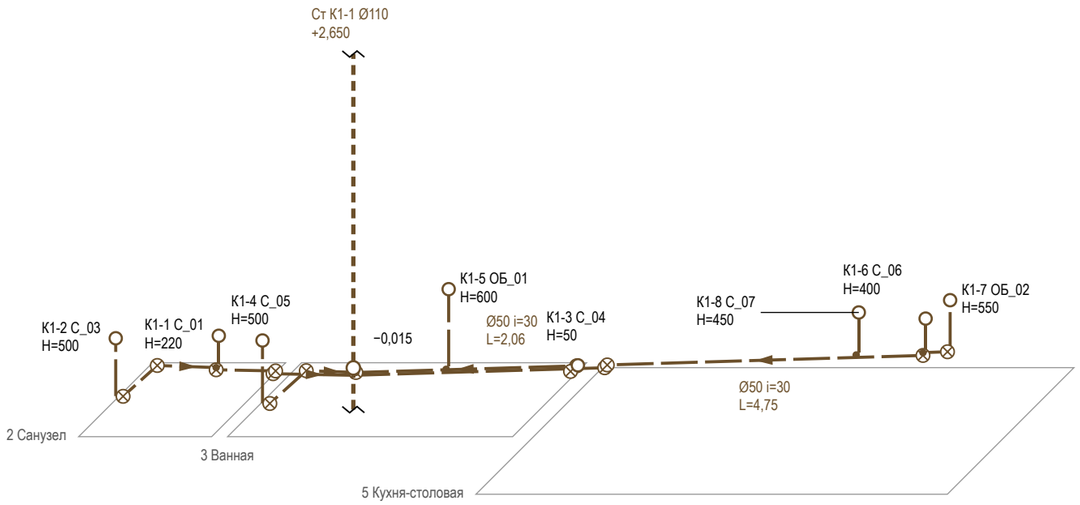

Условные обозначения


- К1 — канализация бытовая
- вывод К1 (код — в ведомости привязок)
- стояк «Ст К1-N / Ст В1-N» (ГОСТ 21.601), Ø мм
- стояк в плане (на отметке пола); вертикаль — стояк по высоте, разрыв — перекрытие
- направление уклона К1 / пола: Ø, мм на 1 м
- ревизия (прочистка) К1 — доступ сохранить
- тройник (ответвление к прибору)
- стояк Т3 не на обмере — принят в шахте рядом со Ст В1, сверить

Примечания


1. Схема К1 построена по тем же трассам, что план разводки: положение в плане сохранено, глубина — в масштабе ×0,5. Трассы принципиальные; фактическое положение фиксируется исполнительной схемой до закрытия.
2. Отметки — от плиты перекрытия: низ трубы у врезки в стояк — отметка из данных выпуска, к прибору труба поднимается на уклон i, мм/м (уклон не менее 1/d и не более 150 мм/м, СП 30.13330.2020, п. 19.1); чистый пол — выше плиты на стяжку (высота пирога пола). Высота выпуска прибора H — от чистого пола.
3. Ревизия — на повороте и в начале участка; стояк К1 в коробе с люком — звукоизоляция стояка в коробе; поворот — двумя отводами 45°.
4. Ст К1-1 на обмере не показаны: положение принято (исполнитель по плану заказчика), не замерено; положение сверить на объекте до разводки.
5. Трубы испытать давлением до закрытия (акт скрытых работ, опрессовка по СП 73.13330.2016).
6. Диаметры, высоты выводов и места кранов — по паспортам выбранных приборов и расчёту проектной организации.
7. Расчёт систем, диаметры магистралей и подбор оборудования выполняет проектная организация.

					Проект: Квартира 68 м², элитный модерн	М 1:50
	Лист	№ док.	Подпись	Дата		
Дизайнер	Кырлан А.С.			04.11.26	Аксонометрическая схема К1 (канализация)	Стадия: П; Лист: 21; Листов: 86

Стена А (М 1:20)

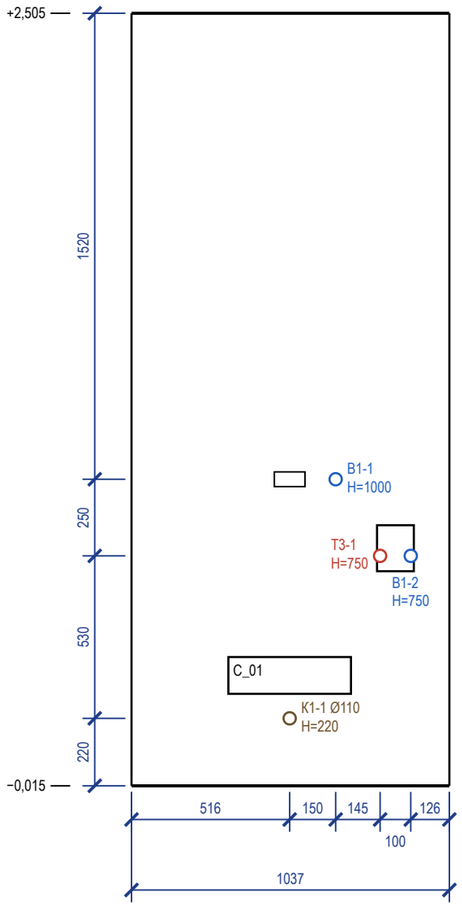

Стена Г (М 1:20)

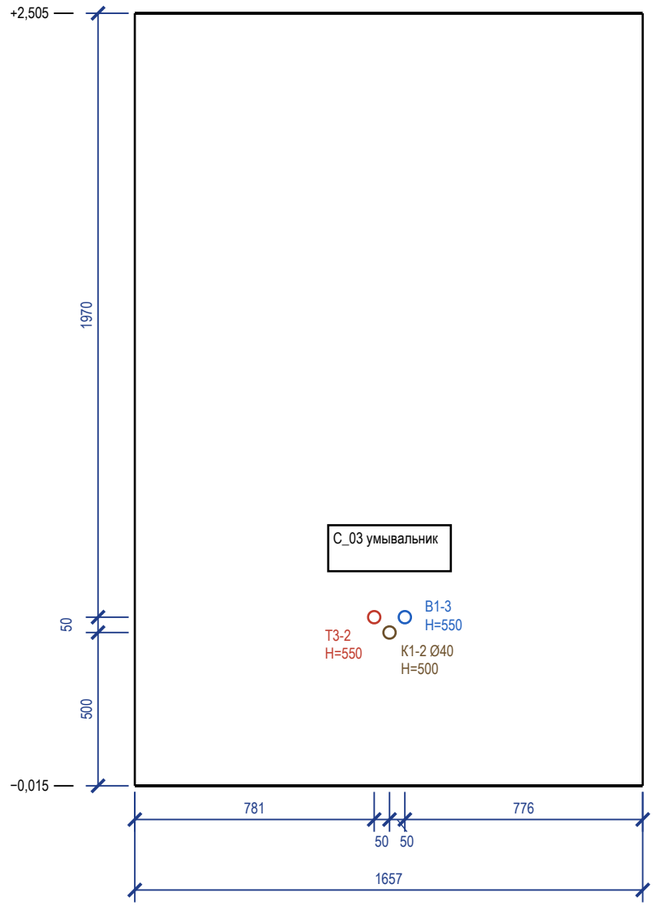

Ведомость привязок выводов (от чистого пола и угла)

Код	Прибор	Ø	H, мм	Привязка, мм
B1-1	C_01 унитаз подвесной	½"	1000	ст. А: 666 от лев. угла
K1-1	C_01 унитаз подвесной	Ø110	220	ст. А: 516 от лев. угла
B1-2	C_02 гигиенический душ	½"	750	ст. А: 911 от лев. угла
T3-1	C_02 гигиенический душ	½"	750	ст. А: 811 от лев. угла
B1-3	C_03 умывальник	½"	550	ст. Г: 881 от лев. угла
T3-2	C_03 умывальник	½"	550	ст. Г: 781 от лев. угла
K1-2	C_03 умывальник	Ø40	500	ст. Г: 831 от лев. угла

Условные обозначения

- вывод B1 (код — в ведомости привязок)
- вывод T3 (код — в ведомости привязок)
- вывод K1 (код — в ведомости привязок)
- сантехприбор по расстановке (габарит модели)
- дверной проём; окно — сплошной контур
- кнопка смыва инсталляции (H — по данным прибора)

Примечания

1. Габариты и высоты приборов, межосевые смесителей и места кранов — по паспортам выбранных приборов, сверяются до разметки стен.
2. Высоты H — от чистого пола помещения, мм; отметка чистого пола и потолка — у левого края вида (от ±0,000 объекта). Привязки — от левого чистового угла вида (облицовка стен вычтена), как на развёртках стен.
3. Кнопка смыва C_01 — H=1000 (по данным прибора).
4. Ревизионные люки (арматура и ревизии у C_01, C_02 300×400, стена А у C_01, предложение): привязка к углу — по раскладке плитки, подтверждается обмером.
5. Ревизионные люки к арматуре и ревизиям в данных не заданы: место и размер не определены (записи реестра нет).
6. Расчёт систем водоснабжения и канализации и подбор оборудования выполняет проектная организация; лист задаёт места и высоты выводов.

	Лист	№ док.	Подпись	Дата
Дизайнер	Кырлан А.С.			04.11.26


Проект: Квартира 68 м², элитный модерн — **М 1:20**

Развёртки мокрых зон: выводы ВК. Санузел


Стадия	Лист	Листов
П	22	86

выпуск 04.11.2026 № f0db2de63c · стр. 22 из 86

Стена А (М 1:20)

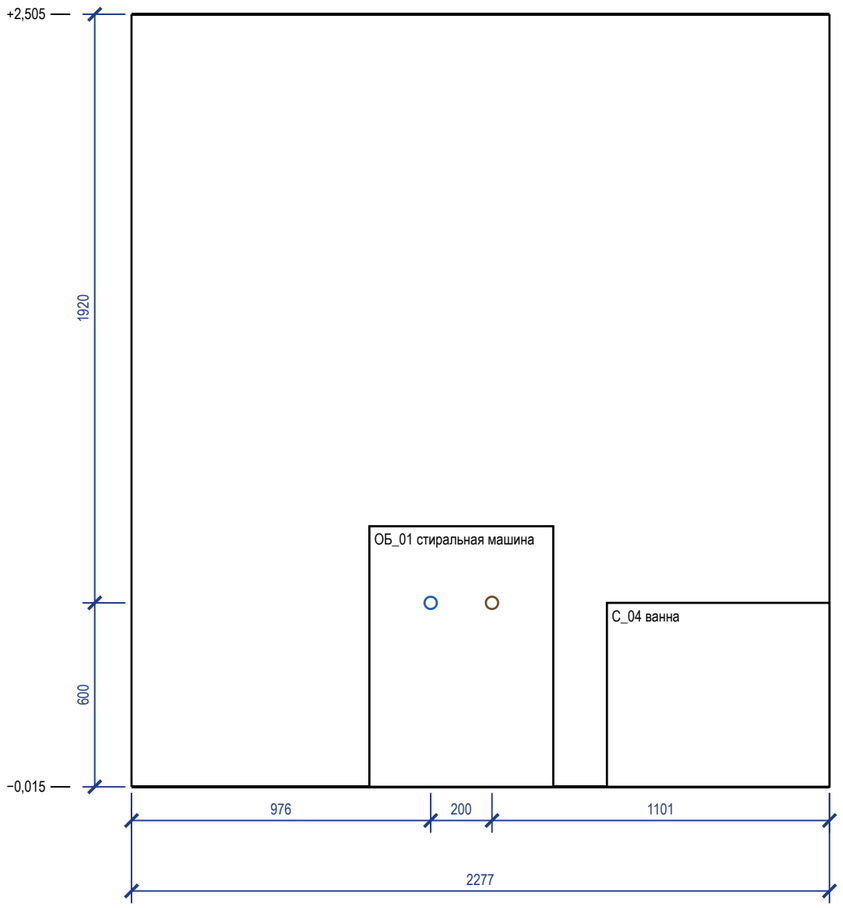

Стена Б (М 1:20)

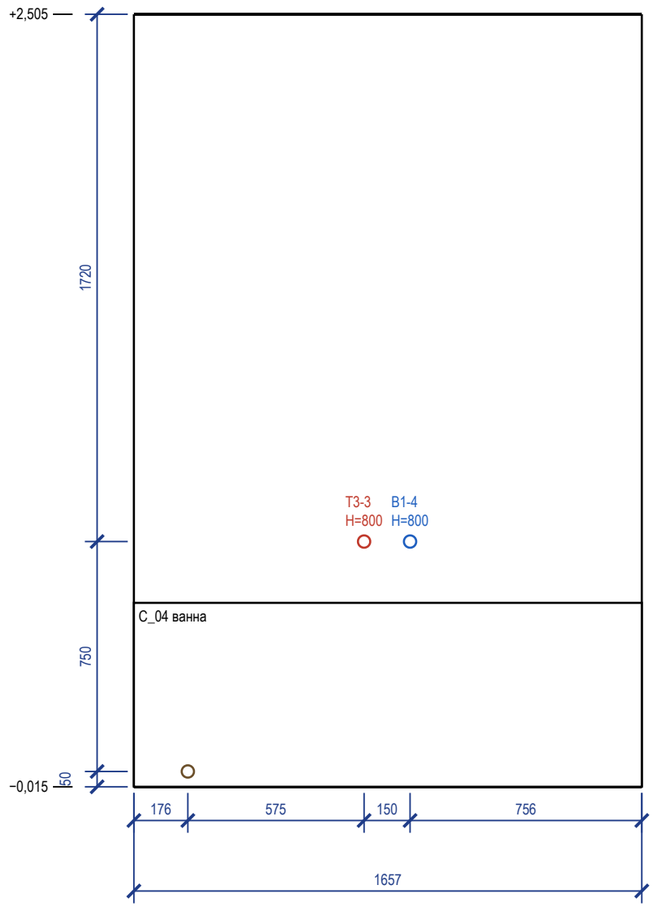

Ведомость привязок выводов (от чистого пола и угла)

Код	Прибор	Ø	H, мм	Привязка, мм
В1-6	ОБ_01 стиральная машина	½"	600	ст. А: 976 от лев. угла
К1-5	ОБ_01 стиральная машина	Ø40	600	ст. А: 1176 от лев. угла
В1-4	С_04 ванна	½"	800	ст. Б: 901 от лев. угла
Т3-3	С_04 ванна	½"	800	ст. Б: 751 от лев. угла
К1-3	С_04 ванна	Ø50	50	ст. Б: 176 от лев. угла

Условные обозначения

- вывод В1 (код — в ведомости привязок)
- вывод Т3 (код — в ведомости привязок)
- вывод К1 (код — в ведомости привязок)
- сантехприбор по расстановке (габарит модели)
- дверной проём; окно — сплошной контур


Примечания

1. Габариты и высоты приборов, межосевые смесителей и места кранов — по паспортам выбранных приборов, сверяются до разметки стен.
2. Высоты H — от чистого пола помещения, мм; отметка чистого пола и потолка — у левого края вида (от ±0,000 объекта). Привязки — от левого чистового угла вида (облицовка стен вычтена), как на развёртках стен.
3. Стояки в помещении: Ст К1-1 Ø110, Ст В1-2 Ø32, Ст Т3-3 Ø32 — положение на плане выводов; выводы подключаются к ним по схеме разводки.
4. Ревизионные люки (С_04 400×300, стена Б, предложение; узел ввода воды (электрокраны ЭК-1, ЭК-2, счётчики, коллектор) 400×600, стена Б у С_04, предложение): привязка к углу — по раскладке плитки, подтверждается обмером.
5. Ревизионные люки к арматуре и ревизиям в данных не заданы: место и размер не определены (записи реестра нет).
6. Часть подписей выводов не уместилась у знака: коды и высоты — в ведомости привязок.
7. Помещение «Ванная» — 2 листа: стены 1) А, Б; 2) В, Г.
8. Расчёт систем водоснабжения и канализации и подбор оборудования выполняет проектная организация; лист задаёт места и высоты выводов.


					Проект: Квартира 68 м², элитный модерн — М 1:20
	Лист	№ док.	Подпись	Дата	
Дизайнер	Кырлан А.С.			04.11.26	Развёртки мокрых зон: выводы ВК. Ванная (лист 1 из 2)

Стадия	Лист	Листов
П	23	86

Стена В (М 1:20)

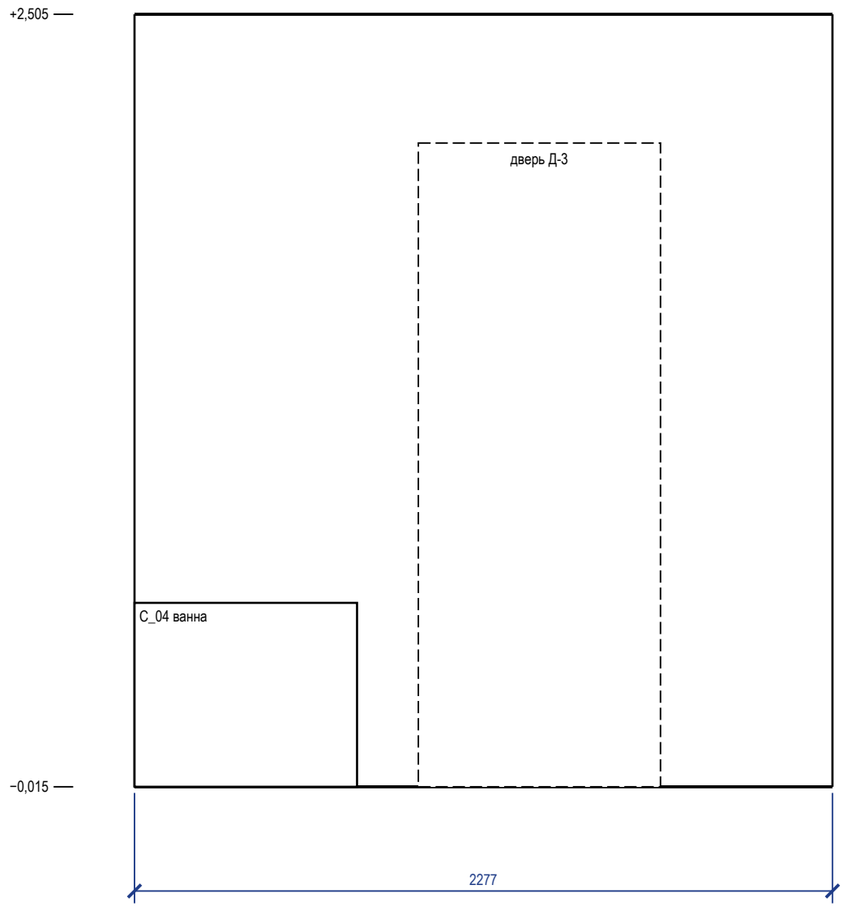

Стена Г (М 1:20)

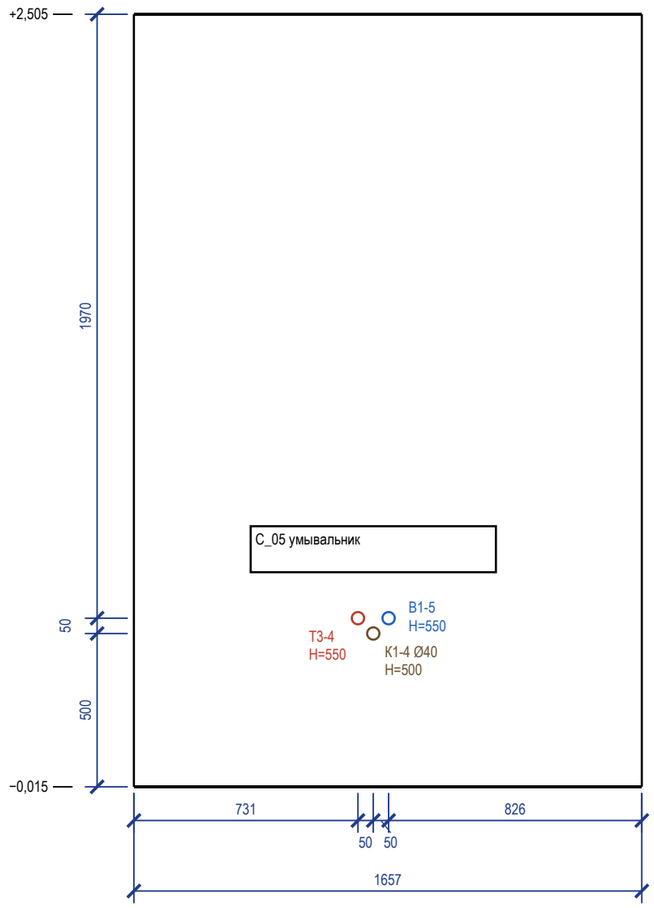

Ведомость привязок выводов (от чистого пола и угла)

Код	Прибор	Ø	H, мм	Привязка, мм
В1-5	С_05 умывальник	½"	550	ст. Г: 831 от лев. угла
Т3-4	С_05 умывальник	½"	550	ст. Г: 731 от лев. угла
К1-4	С_05 умывальник	Ø40	500	ст. Г: 781 от лев. угла

Условные обозначения

- вывод В1 (код — в ведомости привязок)
- вывод Т3 (код — в ведомости привязок)
- вывод К1 (код — в ведомости привязок)
- сантехприбор по расстановке (габарит модели)
- дверной проём; окно — сплошной контур


Примечания

1. Габариты и высоты приборов, межосевые смесителей и места кранов — по паспортам выбранных приборов, сверяются до разметки стен.
2. Высоты H — от чистого пола помещения, мм; отметка чистого пола и потолка — у левого края вида (от ±0,000 объекта). Привязки — от левого чистового угла вида (облицовка стен вычтена), как на развёртках стен.
3. Стояки в помещении: Ст К1-1 Ø110, Ст В1-2 Ø32, Ст Т3-3 Ø32 — положение на плане выводов; выводы подключаются к ним по схеме разводки.
4. Ревизионные люки (С_04 400×300, стена Б, предложение; узел ввода воды (электрокраны ЭК-1, ЭК-2, счётчики, коллектор) 400×600, стена Б у С_04, предложение): привязка к углу — по раскладке плитки, подтверждается обмером.
5. Ревизионные люки к арматуре и ревизиям в данных не заданы: место и размер не определены (записи реестра нет).
6. Помещение «Ванная» — 2 листа: стены 1) А, Б; 2) В, Г.
7. Расчёт систем водоснабжения и канализации и подбор оборудования выполняет проектная организация; лист задаёт места и высоты выводов.

					Проект: Квартира 68 м², элитный модерн — М 1:20
	Лист	№ док.	Подпись	Дата	
Дизайнер	Кырлан А.С.			04.11.26	Развёртки мокрых зон: выводы ВК. Ванная (лист 2 из 2)

Стадия	Лист	Листов
П	24	86

Стена А (М 1:20)

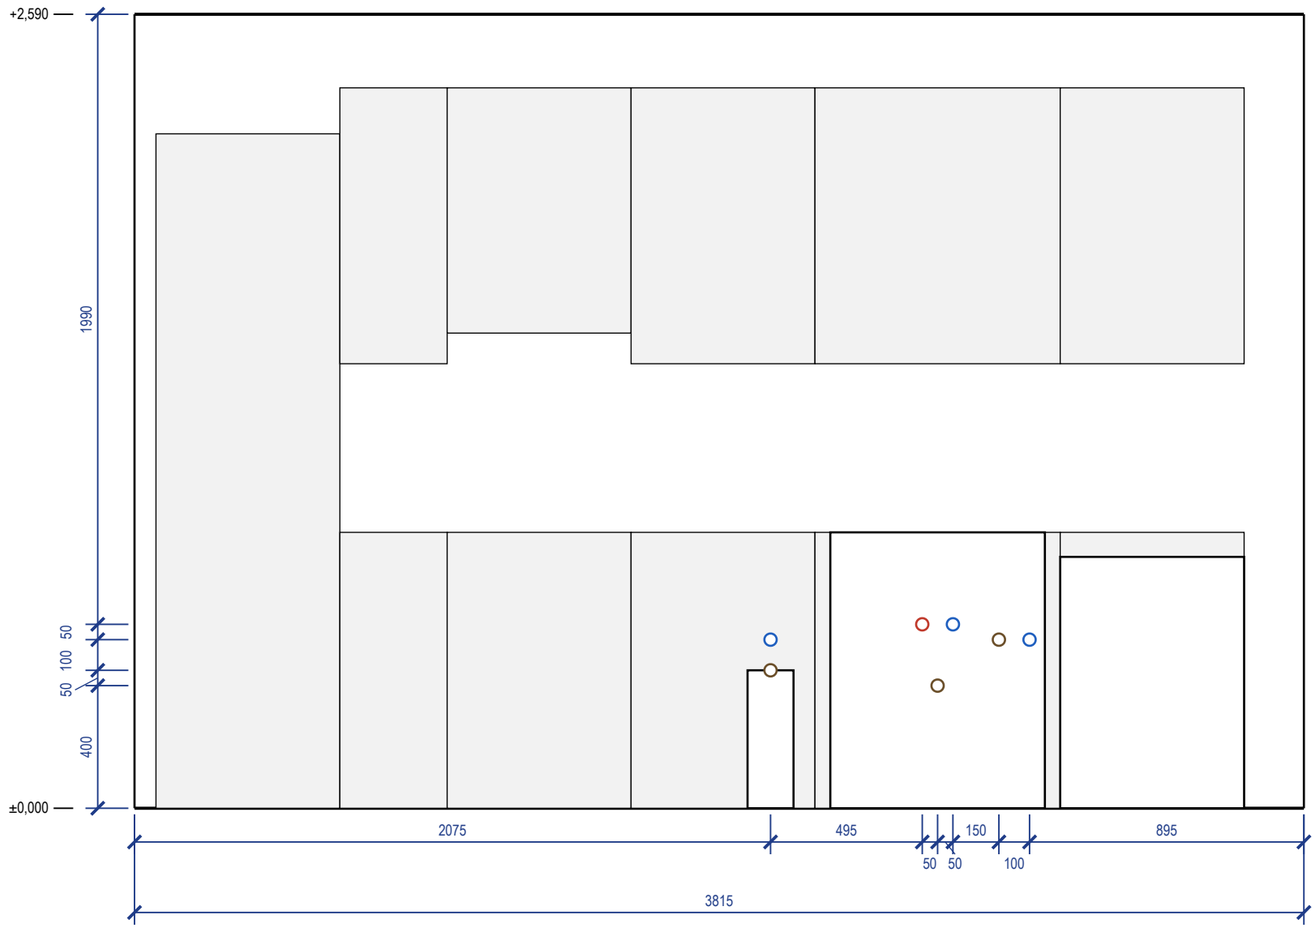

Ведомость привязок выводов (от чистого пола и угла)

Код	Прибор	Ø	H, мм	Привязка, мм
В1-7	С_06 мойка кухонная	½"	600	ст. А: 2670 от лев. угла
Т3-5	С_06 мойка кухонная	½"	600	ст. А: 2570 от лев. угла
К1-6	С_06 мойка кухонная	Ø50	400	ст. А: 2620 от лев. угла
В1-8	ОБ_02 посудомоечная машина	½"	550	ст. А: 2920 от лев. угла

Ведомость привязок (продолжение)

Код	Прибор	Ø	H, мм	Привязка, мм
К1-7	ОБ_02 посудомоечная машина	Ø40	550	ст. А: 2820 от лев. угла
В1-9	С_07 фильтр обратного осмоса	½"	550	ст. А: 2075 от лев. угла
К1-8	С_07 фильтр обратного осмоса	Ø40	450	ст. А: 2075 от лев. угла

Условные обозначения

- вывод В1 (код — в ведомости привязок)
- вывод Т3 (код — в ведомости привязок)
- вывод К1 (код — в ведомости привязок)
- сантехприбор по расстановке (габарит модели)
- дверной проём; окно — сплошной контур

Примечания

1. Габариты и высоты приборов, межосевые смесители и места кранов — по паспортам выбранных приборов, сверяются до разметки стен.
2. Высоты H — от чистого пола помещения, мм; отметка чистого пола и потолка — у левого края вида (от ±0,000 объекта). Привязки — от левого чистового угла вида (облицовка стен вычтена), как на развёртках стен.
3. Ревизионные люки (арматура и ревизии у С_06, ОБ_02, С_07 300×400, стена А у С_06, предложение): привязка к углу — по раскладке плитки, подтверждается обмером.
4. Ревизионные люки к арматуре и ревизиям в данных не заданы: место и размер не определены (записи реестра нет).
5. Мойка, ПММ и фильтр — выводы в шкафу мойки; диаметры и положение сифона и кранов сверить по паспортам приборов и чертежам модуля.
6. Часть подписей выводов не уместилась у знака: коды и высоты — в ведомости привязок.
7. Расчёт систем водоснабжения и канализации и подбор оборудования выполняет проектная организация; лист задаёт места и высоты выводов.

					Проект: Квартира 68 м², элитный модерн — М 1:20
	Лист	№ док.	Подпись	Дата	
Дизайнер	Кырлан А.С.			04.11.26	Развёртки мокрых зон: выводы ВК. Кухня-столовая
					Стадия: П · Лист: 25 · Листов: 86


Поз.	Наименование и техническая характеристика	Тип, марка, обозначение документа	Код продукции	Поставщик	Ед. изм.	Кол.	Масса 1 ед., кг	Примечание
	Санитарные приборы							
1	Ванна встраиваемая акриловая 1700×750 мм, с каркасом, экраном и отверстием слив-перелив	акриловая 1700×750, смеситель настенный		выбор заказчика	шт	1		С_04
2	Унитаз подвесной безободковый, с сиденьем микролифт, крепёж и звукоизолирующая прокладка	инсталляция 1120 + подвесной унитаз		выбор заказчика	шт	1		С_01
3	Инсталляция для подвесного унитаза: рама высотой 1120 мм, бачок, клавиша смыва (ось клавиши 1050 мм от чистого пола)	аналог		выбор заказчика	шт	1		С_01; короб ГКЛВ
4	Умывальник подвесной 400×280 мм, с отверстием под смеситель и переливом	раковина подвесная 400 × 280, смеситель на раковине аналог по характеристикам		выбор заказчика	шт	1		С_03
5	Раковина накладная 800×500 мм, на столешницу тумбы, с переливом	раковина-столешница на подвесной тумбе 800 × 500, смеситель на раковине аналог по характеристикам		выбор заказчика	шт	1		С_05
6	Мойка врезная, нержавеющая сталь 700×480 мм, с переливом	аналог		с кухонной мебелью	шт	1		С_06
7	Фильтр обратного осмоса под мойку, с отдельным краном и врезкой дренажа	аналог		выбор заказчика	шт	1		С_07
	Смесители, сифоны и арматура приборов							
8	Смеситель для ванны настенный однорычажный, межосевое 150 мм, с душевым набором (лейка, шланг, держатель)	аналог		выбор заказчика	шт	1		С_04
9	Смеситель для умывальника однорычажный, с донным клапаном	аналог		выбор заказчика	шт	1		С_03
10	Смеситель для накладной раковины однорычажный, высокий излив, с донным клапаном	аналог		выбор заказчика	шт	1		С_05
11	Смеситель кухонный однорычажный, высокий излив	аналог		выбор заказчика	шт	1		С_06
12	Обвязка ванны слив-перелив Ø40/50 с сифоном	аналог		выбор заказчика	шт	1		С_04
13	Сифон для умывальника бутылочный Ø32/40–50, с гофрой к выпуску	аналог		выбор заказчика	шт	2		С_03, С_05
14	Сифон для мойки Ø40/50	аналог		выбор заказчика	шт	1		С_06
15	Сифон для посудомоечной машины с обратным клапаном, на выводе слива Ø40	аналог		выбор заказчика	шт	1		ОБ_02
16	Сифон для стиральной машины встраиваемый в стену Ø50, с обратным клапаном	аналог		выбор заказчика	шт	1		ОБ_01
17	Кран угловой ½"×½" с гибкой подводкой 40 см (умывальники, мойка)	аналог		выбор заказчика	шт	6		по 2 на прибор
18	Кран шаровой угловой ½"×¾" для подключения стиральной и посудомоечной машины	аналог		выбор заказчика	шт	2		ОБ_01, ОБ_02
	Трубопроводы							
19	Труба полипропиленовая PP-R PN20 Ø20×3,4 (В1)	ГОСТ 32415-2013		выбор заказчика	м	17,5	0,17	9,8 + 6,0 + 10 %
20	Труба PP-R, армированная стекловолокном, PN20 Ø20×2,8 (Т3)	ГОСТ 32415-2013		выбор заказчика	м	14	0,15	9,1 + 3,3 + 10 %
21	Труба канализационная ПП Ø40 (К1)	ГОСТ 32414-2013		выбор заказчика	м	6,5		3,0 + 2,6 + 10 %
22	Труба канализационная ПП Ø50 (К1)	ГОСТ 32414-2013		выбор заказчика	м	8		6,8 + 0,5 + 10 %
23	Труба канализационная ПП Ø110 (К1)	ГОСТ 32414-2013		выбор заказчика	м	2		1,3 + 0,2 + 10 %
	Фасонные части и выводы							
24	Отвод канализационный ПП 45° Ø40	ГОСТ 32414-2013		выбор заказчика	шт	10		2 шт. на поворот
25	Отвод канализационный ПП 45° Ø50	ГОСТ 32414-2013		выбор заказчика	шт	12		2 шт. на поворот
26	Отвод канализационный ПП 45° Ø110	ГОСТ 32414-2013		выбор заказчика	шт	6		2 шт. на поворот
27	Тройник канализационный ПП 45° (врезки ветвей)	ГОСТ 32414-2013		выбор заказчика	шт	7		
28	Ревизия канализационная ПП (после поворота трассы)	ГОСТ 32414-2013		выбор заказчика	шт	8		доступ сохранить
29	Фитинги PP-R Ø20: тройники, угольники 90° (ветви и повороты В1, Т3)	ГОСТ 32415-2013		выбор заказчика	шт	23		
30	Водорозетка PP-R Ø20×½" настенная, с креплением	ГОСТ 32415-2013		выбор заказчика	шт	14		коды — лист выводов
	Узлы ввода, люки, короба							
31	Кран шаровой латунный Ду15 PN16 (отключение ввода)	аналог		выбор заказчика	шт	2		Ст В1-2, Ст Т3-3
32	Фильтр сетчатый косой Ду15	аналог		выбор заказчика	шт	2		
33	Счётчик воды крыльчатый Ду15 (ХВ, ГВ), с поверкой	аналог		выбор заказчика	шт	2		пломба УК
34	Клапан обратный Ду15	аналог		выбор заказчика	шт	2		
35	Люк ревизионный нажимной под плитку 300×400 мм	аналог		выбор заказчика	шт	4		к стоякам и арматуре
36	Звукоизоляция стояка К1 в коробе: рулонный звукоизоляционный материал ≥ 10 мм, обмотка стояка на высоту этажа	аналог		выбор заказчика	м	2,7		Ст К1-1
37	Короб К1 над полом: профиль ПН/ПС, ГКЛВ 12,5 мм под плитку	аналог		выбор заказчика	м	2,3		сечение — лист разводки


Примечания

1. Форма 1 ГОСТ 21.110-2013, ширины граф изменены по п. 4.1. «Аналог» — аналог по характеристикам: модели внести до черновых работ, привязки выводов сверить по паспортам.
2. Бытовая техника не входит (показана арматура подключения), мойка — в комплекте кухни (марка — модуля кухни, как у столяра). Длины труб — трасса листа разводки + подъёмы + 10 %.
3. Стояк К1 в коробе — звукоизоляция стояка в коробе без жёсткого контакта короба с трубой.
4. Расчёт систем водоснабжения и канализации, диаметры магистралей и подбор оборудования выполняет проектная организация.

					Проект: Квартира 68 м², элитный модерн
	Лист	№ док.	Подпись	Дата	
Дизайнер	Кырлан А.С.			04.11.26	Спецификация сантехнического оборудования

Стадия	Лист	Листов
П	26	86

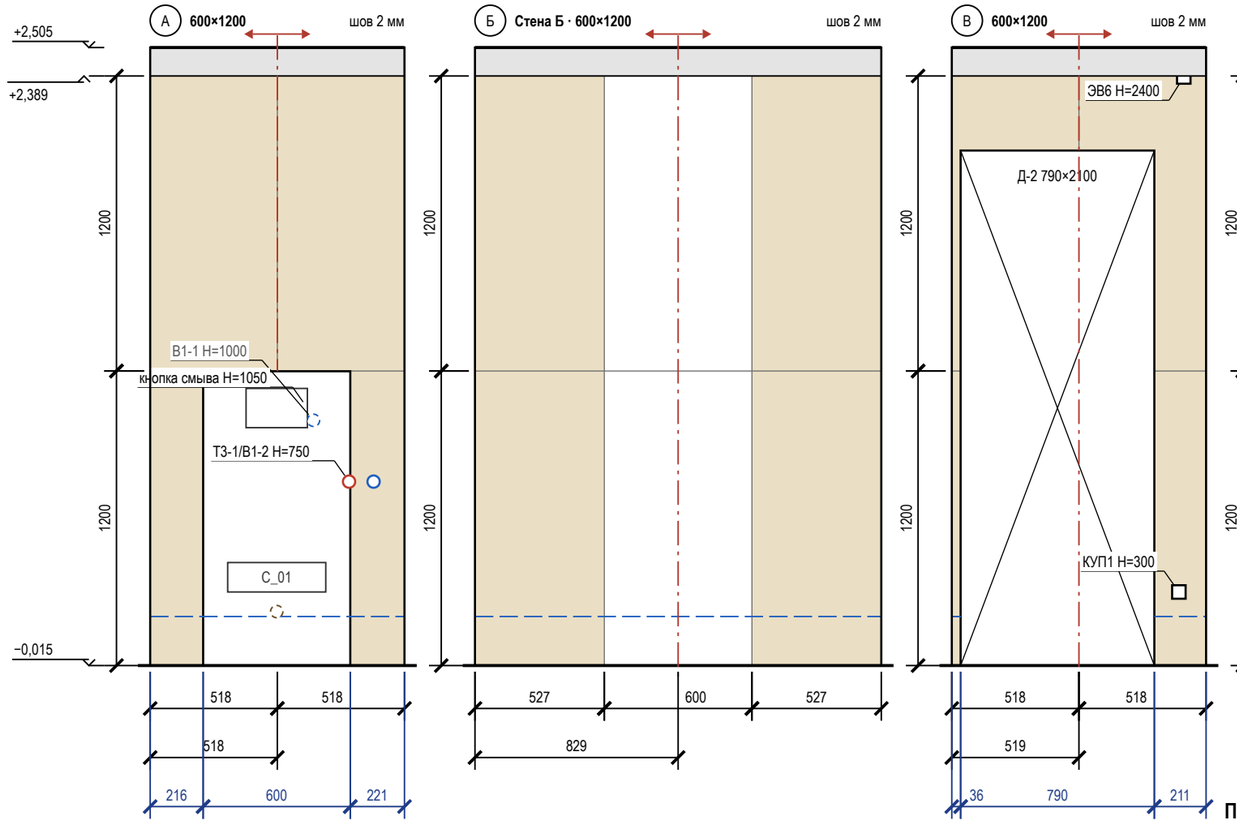

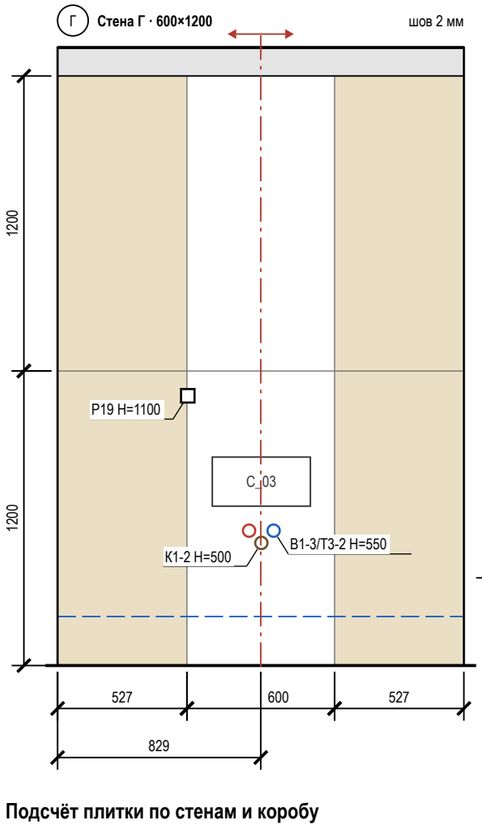

Условные обозначения

- плитка целая; тонкая линия — шов
- плитка с подрезкой (размер — на цепочке)
- ось старта; стрелки — направление укладки
- верх гидроизоляции: 200 от ЧП, в мокрой зоне — «до …»
- проём — не облицовывается
- сантехприбор: габарит, высота по практике
- короб инсталляции, в нём кнопка смыва 250×160
- вывод В1 (код — в ведомости привязок)
- вывод Т3 (код — в ведомости привязок)
- вывод К1 (код — в ведомости привязок)
- вывод за прибором / в коробе (не на сетке)
- электроточка: марка и Н — по листам ЭОМ
- отметка уровня, м: ±0,000 — чистый пол жилых помещений
- низ потолка; серая полоса — стена без плитки
- (А) обозначение стены А–Г (как на развёртках)

Подсчёт плитки по стенам и коробу

Поверхность	L × H, мм	S, м²	Целых	Подр.	С запасом	Подрезки: край / верх, мм
стена А	1037 × 2404	1,89	0	4	5	518 / 518; целый ряд
короб (ст. А)	600×1200×250	1,47	1	3	5	лицо 600; бок. 250
стена Б	1657 × 2404	4,10	2	4	7	527 / 527; целый ряд
стена В	1037 × 2404	0,95	0	4	5	518 / 518; целый ряд
стена Г	1657 × 2404	4,10	2	4	7	527 / 527; целый ряд
Итого		**12,51**	**5**	**19**	**29**	

Сдвиг точек под раскладку


Точка (ВК, ЭОМ)	Стена	Проект: от угла / Н	Под раскладку: от угла / Н	Сдвиг, мм
ЭВ6	В	946 / 2400	819 / 2400	−127 в центр плитки
КУП1	В	926 / 300	819 / 300	−107 в центр плитки

Примечания

1. Вид изнутри, стены по часовой стрелке А → Г. Высоты — от чистого пола (−0,015), отметки — от ±0,000. Раскладка от чистовых размеров (штукатурка 10 + клей 5 + плитка 9 мм), подрезки чистые; старт — от оси стены, ряды от пола целыми.
2. Верх плитки +2,389, потолок +2,505, зазор 116 мм: потолок ГКЛ опустить до +2,392 (шов 3 мм, герметик) — согласовать с монтажником ГКЛ; иначе профиль-окантовка, полосу окрасить в цвет потолка. Подрезной ряд 111 мм не делать.
3. Точки из таблицы сдвигов переносятся до черновой разводки (ЭОМ — по тем же числам).
4. Выводы ВК стоят по оси прибора и с прибором не двигаются — привязки по «Плану выводов сантехники» без сдвига; вне сетки (Т3-1/В1-2) — отверстие в плитке коронкой по той же привязке, плитку не сдвигать.
5. За приборами и в коробе (В1-1, К1-1) — штриховым кольцом.
6. Гидроизоляция: 200 мм от ЧП по периметру; углы — лентой; акт скрытых работ, пролив.
7. Короб 600×1200×250: лицо 600 мм от оси кнопки смыва, боковины, полка; углы — запил 45° или профиль; за коробом плитку не кладут.

					Проект: Квартира 68 м², элитный модерн	**М 1:25**
	Лист	№ док.	Подпись	Дата		
Дизайнер	Кырлан А.С.			04.11.26	Раскладка плитки. Санузел. Развёртки стен	Стадия: П; Лист: 27; Листов: 86

выпуск 04.11.2026 № f0db2de63c · стр. 27 из 86

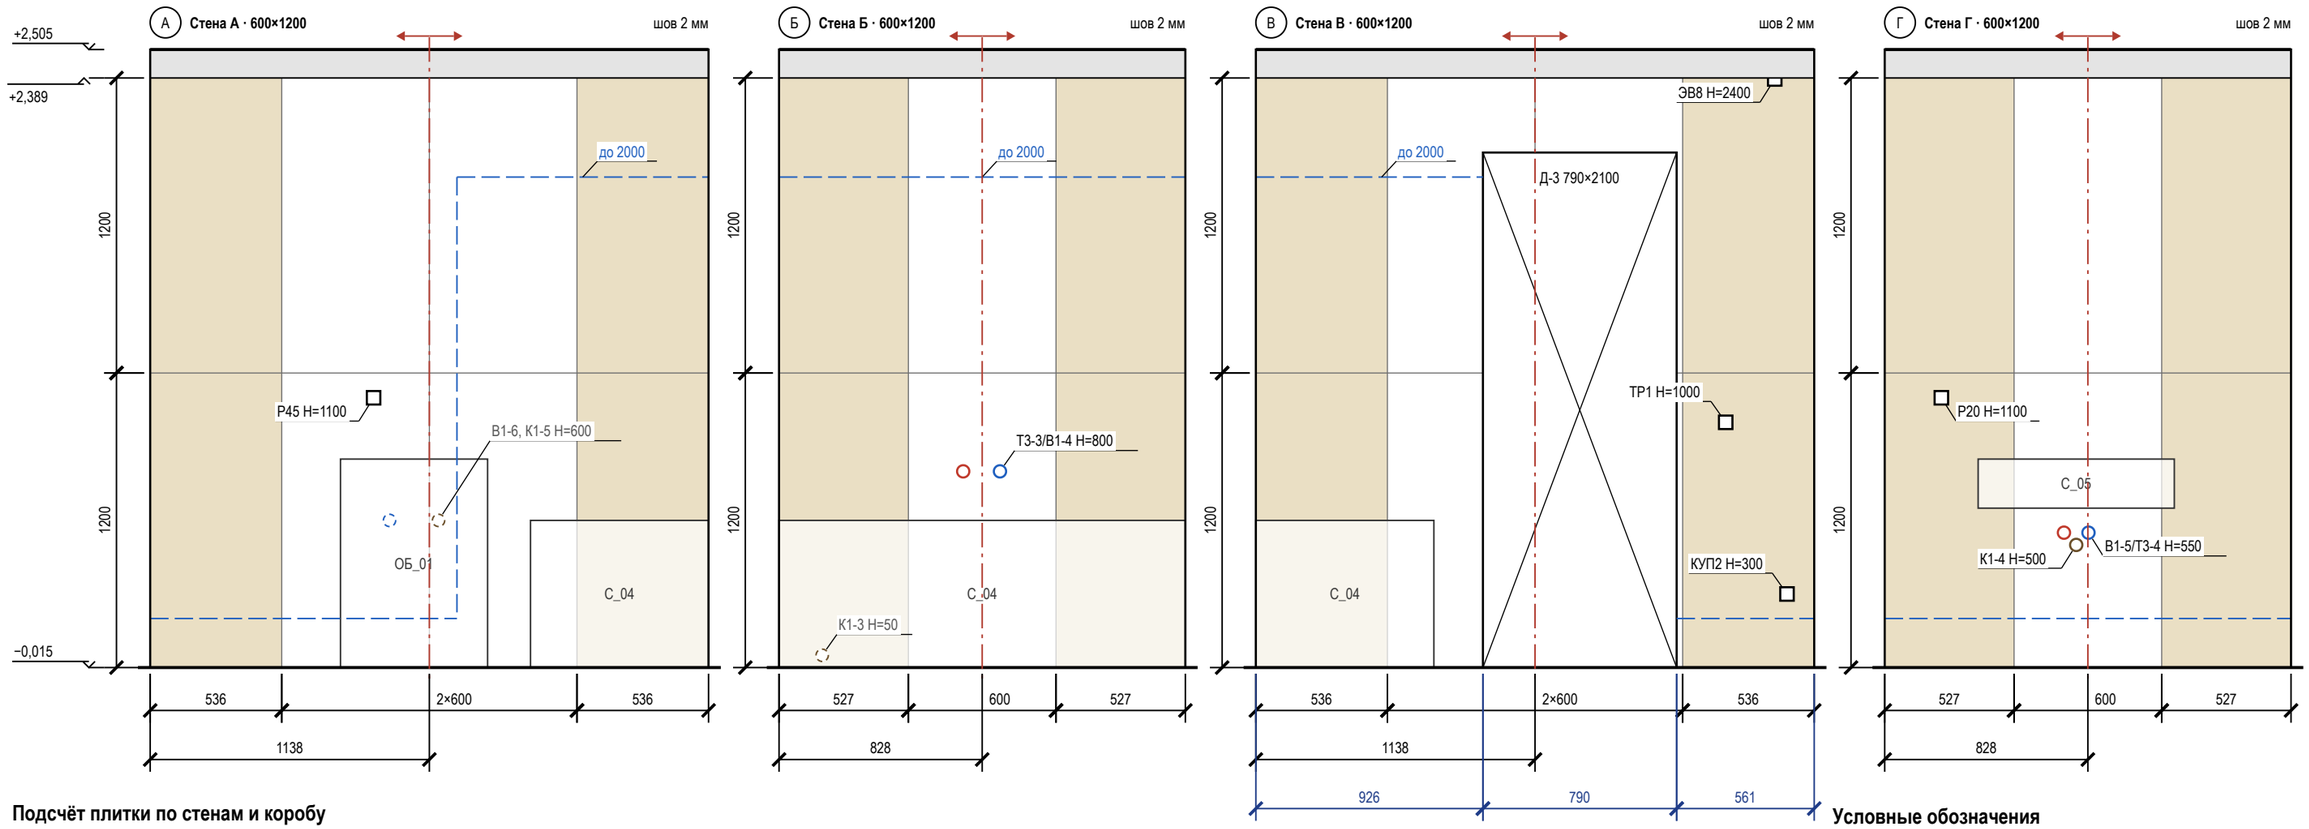

Подсчёт плитки по стенам и коробу

Поверхность	L × H, мм	S, м²	Целых	Подр.	С запасом	Подрезки: край / верх, мм
стена А	2277 × 2404	5,59	4	4	9	536 / 536; целый ряд
стена Б	1657 × 2404	4,10	2	4	7	527 / 527; целый ряд
стена В	2277 × 2404	3,93	0	8	9	536 / 536; целый ряд
стена Г	1657 × 2404	4,10	2	4	7	527 / 527; целый ряд
Итого		**17,72**	**8**	**20**	**32**	

Сдвиг точек под раскладку

Точка (ВК, ЭОМ)	Стена	Проект: от угла / H	Под раскладку: от угла / H	Сдвиг, мм
Р45	А	911 / 1100	838 / 1100	−73 в центр плитки
ЭВ8	В	2116 / 2400	2041 / 2400	−75 в центр плитки
КУП2	В	2166 / 300	2041 / 300	−125 в центр плитки
ТР1	В	1916 / 1000	2041 / 1000	+125 в центр плитки

Примечания

1. Вид изнутри, стены по часовой стрелке А → Г. Высоты — от чистого пола (−0,015), отметки — от ±0,000. Раскладка от чистовых размеров (штукатурка 10 + клей 5 + плитка 9 мм), подрезки чистые; старт — от оси стены, ряды от пола целыми.
2. Верх плитки +2,389, потолок +2,505, зазор 116 мм: потолок ГКЛ опустить до +2,392 (шов 3 мм, герметик) — согласовать с монтажником ГКЛ; иначе профиль-окантовка, полосу окрасить в цвет потолка. Подрезной ряд 111 мм не делать.
3. Точки из таблицы сдвигов переносятся до черновой разводки (ЭОМ — по тем же числам).
4. Выводы ВК стоят по оси прибора и с прибором не двигаются — привязки по «Плану выводов сантехники» без сдвига; вне сетки (В1-5/Т3-4, К1-4) — отверстие в плитке коронкой по той же привязке, плитку не сдвигать.
5. За приборами и в коробе (В1-6, К1-5, К1-3) — штриховым кольцом.
6. Гидроизоляция: 200 мм от ЧП по периметру; над ванной — до 2000 и 300 мм за борт (СП 29.13330.2011, п. 7.2 — на высоту замачивания); углы — лентой; акт скрытых работ, пролив.

Условные обозначения

- плитка целая; тонкая линия — шов
- плитка с подрезкой (размер — на цепочке)
- ось старта; стрелки — направление укладки
- верх гидроизоляции: 200 от ЧП, в мокрой зоне — «до …»
- проём — не облицовывается
- сантехприбор: габарит, высота по практике
- вывод В1 (код — в ведомости привязок)
- вывод Т3 (код — в ведомости привязок)
- вывод К1 (код — в ведомости привязок)
- вывод за прибором / в коробе (не на сетке)
- электроточка: марка и H — по листам ЭОМ
- отметка уровня, м: ±0,000 — чистый пол жилых помещений
- низ потолка; серая полоса — стена без плитки
- (А) обозначение стены А–Г (как на развёртках)


	Лист	№ док.	Подпись	Дата
Дизайнер	Кырлан А.С.			04.11.26

Проект: Квартира 68 м², элитный модерн — **М 1:25**

Раскладка плитки. Ванная. Развёртки стен

Стадия	Лист	Листов
П	28	86

выпуск 04.11.2026 № f0db2de63c · стр. 28 из 86

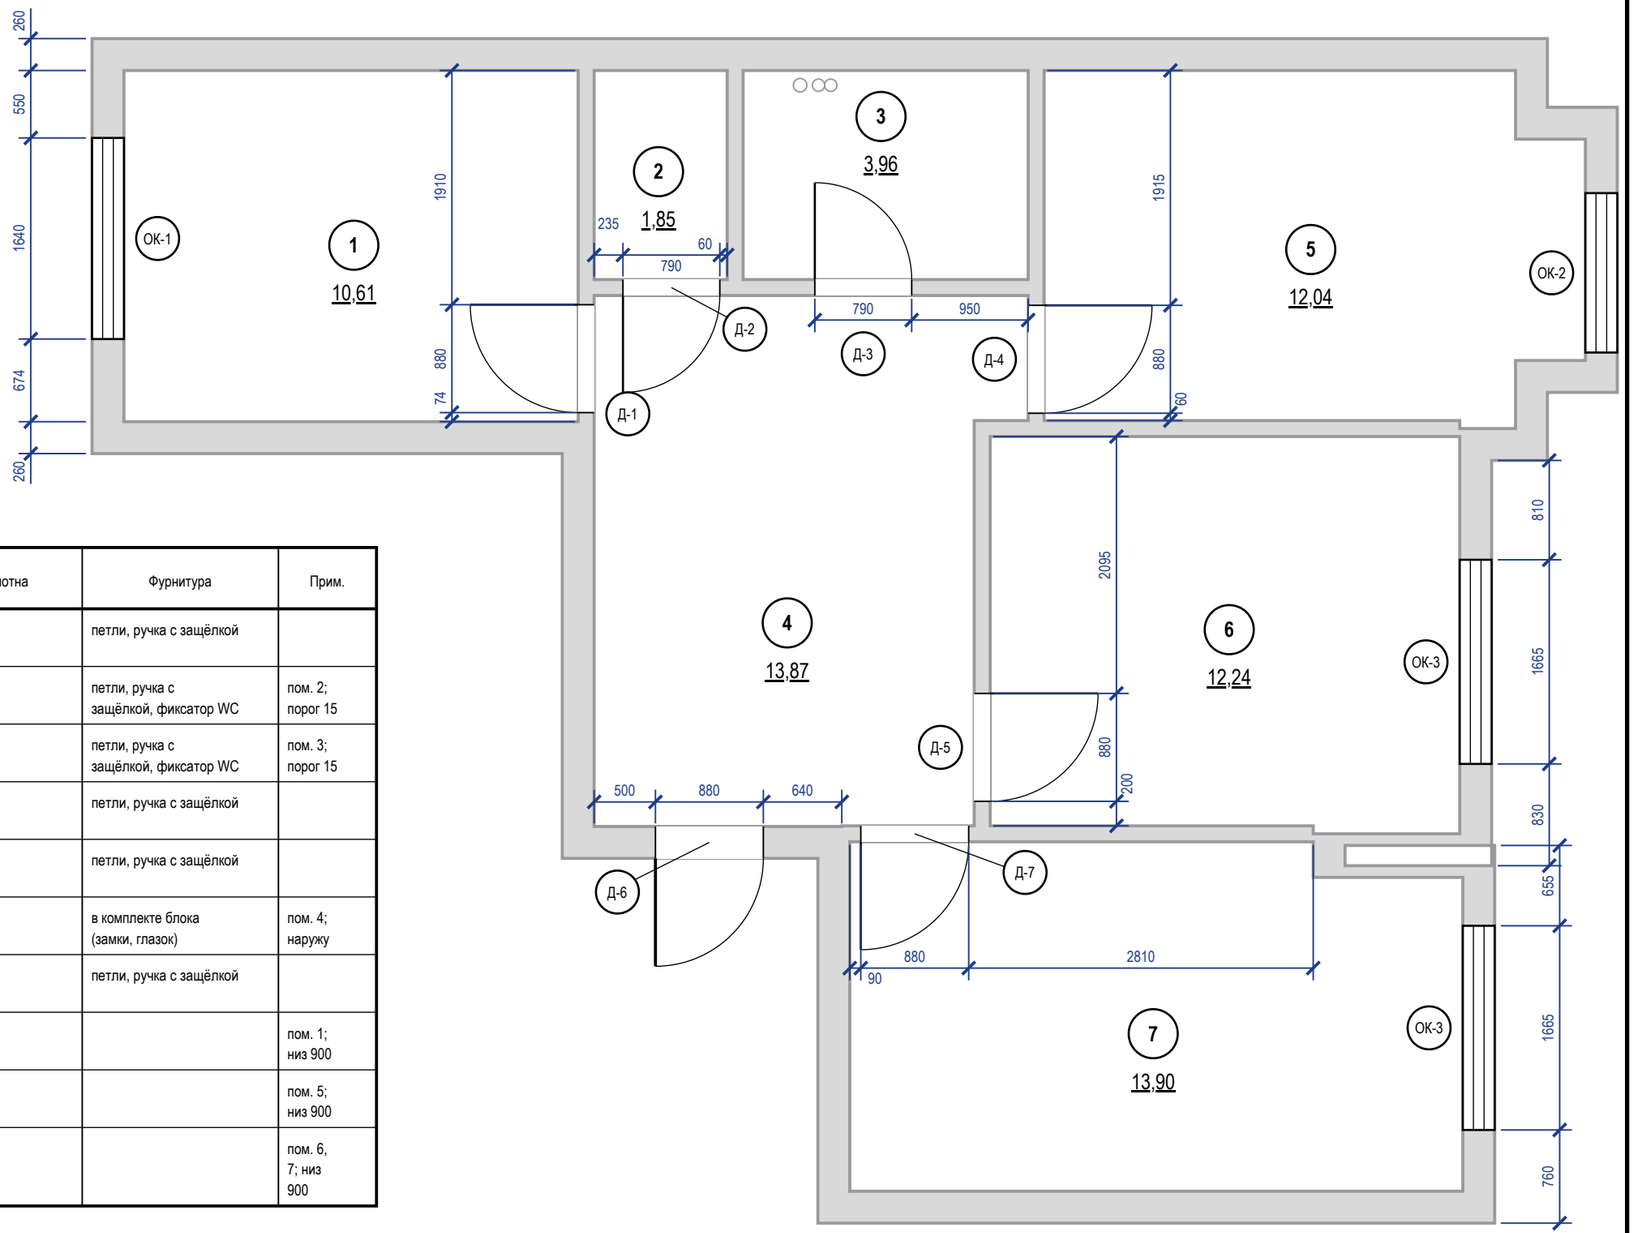

Ведомость заполнения проёмов


Марка	Наименование, обозначение	Проём ш×в, мм	Полотно (расч.)	Кол.	Откр.	Отделка полотна	Фурнитура	Прим.
Д-1	Блок дверной внутренний, ГОСТ 475-2016	880×2100	800×2000	1	Л		петли, ручка с защёлкой	
Д-2	Блок дверной внутренний, ГОСТ 475-2016	790×2100	700×2000	1	Л		петли, ручка с защёлкой, фиксатор WC	пом. 2; порог 15
Д-3	Блок дверной внутренний, ГОСТ 475-2016	790×2100	700×2000	1	П		петли, ручка с защёлкой, фиксатор WC	пом. 3; порог 15
Д-4	Блок дверной внутренний, ГОСТ 475-2016	880×2100	800×2000	1	П		петли, ручка с защёлкой	
Д-5	Блок дверной внутренний, ГОСТ 475-2016	880×2100	800×2000	1	П		петли, ручка с защёлкой	
Д-6	Блок дверной входной, ГОСТ 31173-2016	880×2100	блок задать	1	Л	в комплекте блока	в комплекте блока (замки, глазок)	пом. 4; наружу
Д-7	Блок дверной внутренний, ГОСТ 475-2016	880×2100	800×2000	1	Л		петли, ручка с защёлкой	
ОК-1	Блок оконный, ГОСТ 23166-2021	1640×1500		1				пом. 1; низ 900
ОК-2	Блок оконный, ГОСТ 23166-2021	1300×1500		1				пом. 5; низ 900
ОК-3	Блок оконный, ГОСТ 23166-2021	1665×1500		2				пом. 6, 7; низ 900

Примечания

1. Размеры проёмов и привязки — в миллиметрах от чистых граней стен до отделки; привязка — от угла того помещения, со стороны которого стоит размер. Размер проёма — ширина × высота от чистого пола 0,000. Размеры на плане — проёмов, не полотен: полотно — в ведомости, коробка — по системе.
2. Марки в кружках — типы заполнения проёмов (ГОСТ 21.501-2018, п. 5.3.2); одна марка — один типоразмер; количество сверено с планом.
3. Открывание: Л — петли слева, П — справа, если смотреть со стороны, куда открывается полотно (на себя).
4. Дверные блоки обычного монтажа (Д-1…Д-5, Д-7) заказывать после чистовой стяжки и штукатурки, проёмы перемерить; монтажный зазор коробки 10–15 мм на сторону, откос от угла помещения до коробки не менее 50 мм.
5. Полотно «расч.» — по проёму с запасом по каталогам, заказ — по таблице проёмов модели; Д-1…Д-5, Д-7: проём 2100, а под полотно 2000 по каталогам нужен 2040–2080, под 2100 — 2140–2180: высоту проёма — по модели; Д-6: входной блок по ГОСТ 31173-2016 — задать при выборе блока.
6. Экспликация помещений — лист 6; в марках помещений — номер и площадь, м².

					Проект: Квартира 68 м², элитный модерн	**М 1:50**
	Лист	№ док.	Подпись	Дата		
Дизайнер	Кырлан А.С.			04.11.26	План размещения дверей	Стадия: П; Лист: 29; Листов: 86

выпуск 04.11.2026 № f0db2de63c · стр. 29 из 86

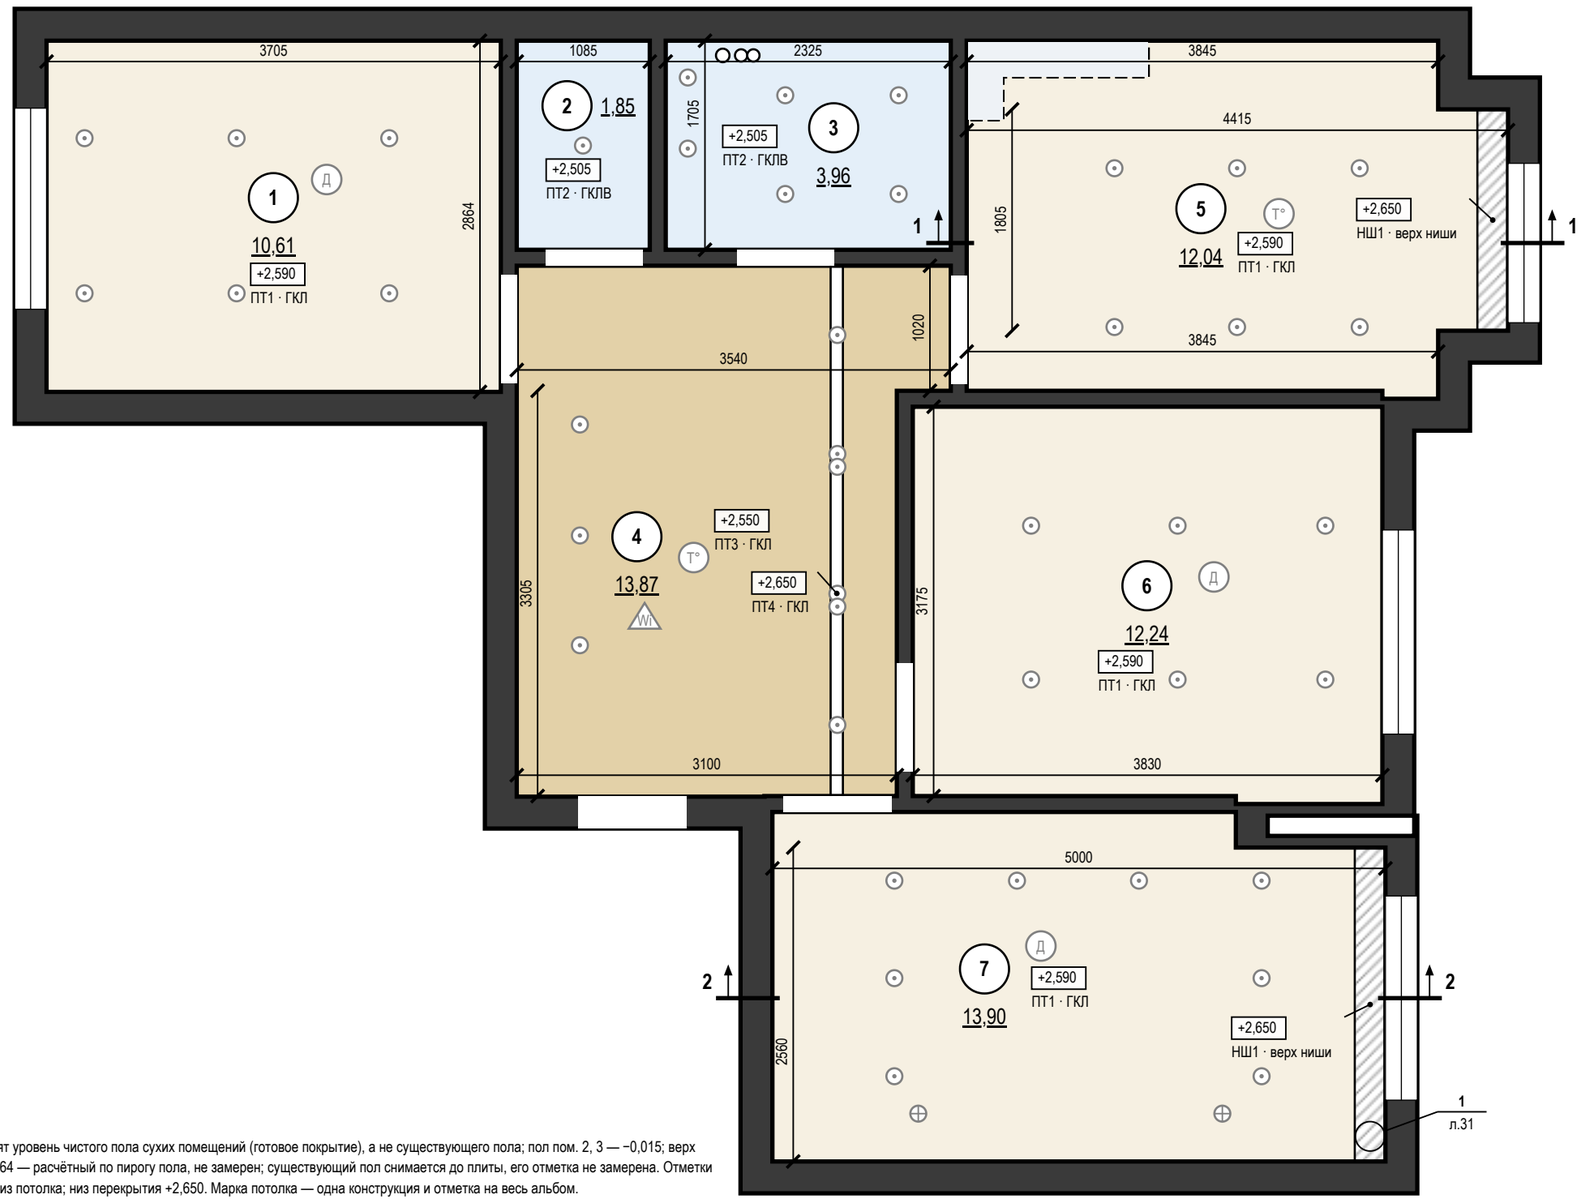

Ведомость потолков

Пом.	Марка	Конструкция	Низ / верх ниши	S, м²	Q
1	ПТ1	ГКЛ П113	+2,590	10,61	Q3
2	ПТ2	ГКЛВ П113	+2,505	1,85	Q3
3	ПТ2	То же	+2,505	3,96	Q3
4	ПТ3	ГКЛ П113	+2,550	13,44	Q3
4	ПТ4	Существующий потолок	+2,650	0,43	
5	ПТ1	ГКЛ П113	+2,590	11,59	Q3
5	НШ1	ниша под шторы 250×60	+2,650	0,45	
6	ПТ1	ГКЛ П113	+2,590	12,24	Q3
7	ПТ1	То же	+2,590	13,26	Q3
7	НШ1	ниша под шторы 250×60	+2,650	0,64	
		Итого		**68,47**	

Ведомость вырезов и закладных в потолке

Марка	Устройство	Кол.	Пом.
	Светильник встраиваемый (марки — план освещения)	42	1, 2, 3, 4, 5, 6, 7
	Светильник подвесной (марки — план освещения)	2	7
ИП1, ИП4, ИП5	Извещатель дымовой	3	1, 6, 7
ИП2, ИП3	Извещатель тепловой	2	4, 5
АР1	Точка доступа Wi-Fi, PoE	1	4

Примечания

1. За отметку ±0,000 принят уровень чистого пола сухих помещений (готовое покрытие), а не существующего пола; пол пом. 2, 3 — −0,015; верх плиты перекрытия −0,064 — расчётный по пирогу пола, не замерен; существующий пол снимается до плиты, его отметка не замерена. Отметки в прямоугольниках — низ потолка; низ перекрытия +2,650. Марка потолка — одна конструкция и отметка на весь альбом.
2. Размеры помещений в свету (ширина × длина, мм), не поместившиеся на плане: пом. 2 — 1085 × 1705; пом. 4 — 3540 × 1020, 3100 × 3305, 2020 × 5; пом. 6 — 3830 × 3175, 1195 × 65; пом. 7 — 3780 × 290, 5000 × 2560.
3. Потолки ГКЛ — каркасная система П113: подвесы через 1000 (с запасом: СП 163, табл. 14 — до 1100 при 0,15 кН/м²), несущие профили через 500, основные через 1200 мм; листы — поперёк несущих профилей. В помещениях 2, 3 — ГКЛВ на оцинкованном каркасе.
4. Ниши под шторы 250×60 мм — на всю длину стены с окном; карниз — на закладной до обшивки (узел 1, лист 31).
5. Примыкание к стенам: теневой шов 15 мм, техзазор 3 мм — пом. 1, 4, 5, 6, 7, по стенам, выровненным штукатуркой (узел 1); пом. 2, 3 разделительная лента.
6. Светильники и потолочные устройства — подложка с планов освещения, слаботочных систем и вентиляции (положение — по ним); вырезы и закладные — по ведомости на листе, до обшивки; отверстия не совмещать с профилями, глубина корпуса светильника до 50 мм.
7. Разрезы 1–1, 2–2 — на листе 31; высоты мебели и дверных блоков сверены с низом потолка в разрезах.
8. Шпаклевание ГКЛ и условия приёмки — Q3: рассеянный дневной свет, осмотр с 2 м; боковой свет не оценивается.
9. Пом. 5: короб воздуховода кухонной вытяжки ГКЛ 300×130 мм (ширина от стены × высота), низ +2,520, длина 1,53 м — по трассе плана вентиляции, вдоль стен до входа в канал; под плоский воздуховод 200×60 (сечение ≈ Ø125): круглый Ø125 в коробе 200 мм опустил бы кухню ниже 2,5 м — сечение подтверждает раздел ОВ; каркас ПН 28×27 по стене и плите, ПП 60×27, лист ГКЛ 12,5.
10. Сечения потолков М 1:10: пом. 5 — 5.1, 5.2 (лист 33); пом. 7 — 5.1, 5.2 (лист 33).

					Проект: Квартира 68 м², элитный модерн — **М 1:50**
	Лист	№ док.	Подпись	Дата	
Дизайнер	Кырлан А.С.			04.11.26	План потолков


Стадия	Лист	Листов
П	30	86

выпуск 04.11.2026 № f0db2de63c · стр. 30 из 86

Правка к этому листу


Разрез 1–1 (М 1:40)

Пом. 5 Кухня-столовая; линия разреза — план потолков, лист 30

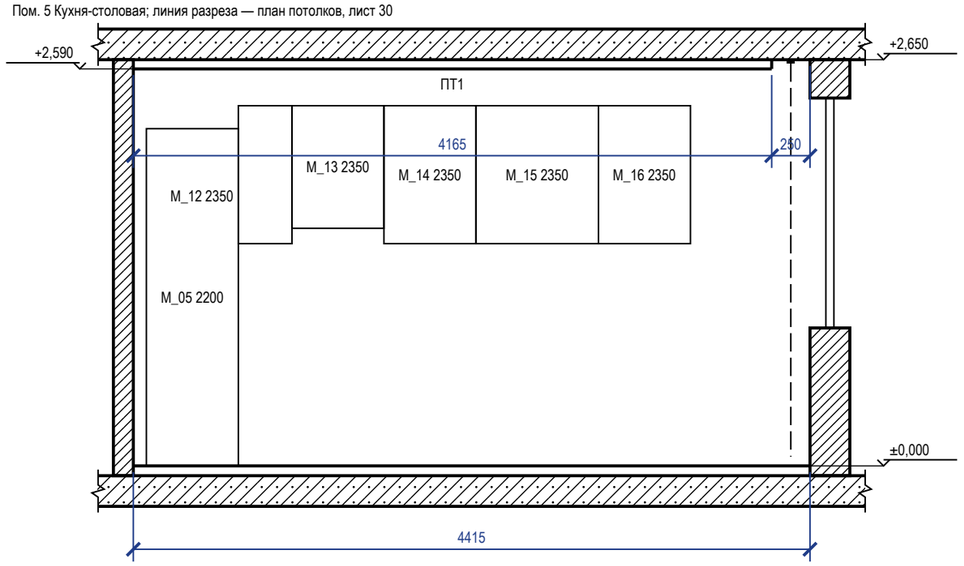

Разрез 2–2 (М 1:40)

Пом. 7 Спальня; линия разреза — план потолков, лист 30

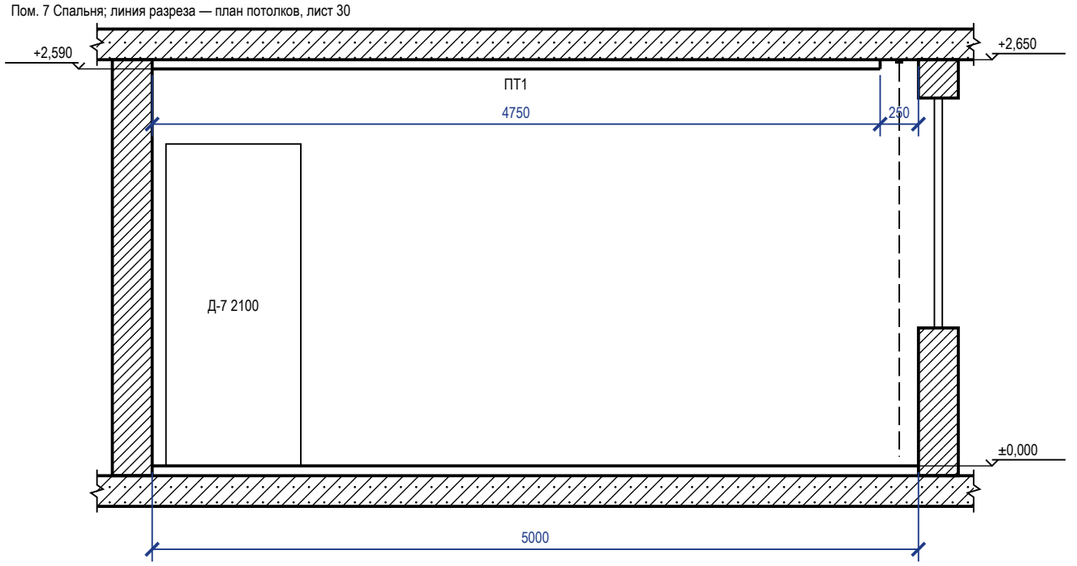

1 Ниша под шторы (М 1:10)

Пом. 5, 7; без подсветки; закладные под карниз — до обшивки

1 — стенка ниши — ГКЛ 12,5
2 — карниз (шина), высота с верхом портьеры 60 мм
3 — ПП 60×27 — каркас короба
4 — низ короба нижнего уровня — ГКЛ 12,5
5 — портьера
6 — стена с окном

Условные обозначения

- плита перекрытия в сечении
- стена в сечении
- потолок ГКЛ в сечении; под линией — марка потолка (план потолков)
- мебель и дверные проёмы за секущей плоскостью; число — марка и верх от чистого пола, мм
- портьера в нише под шторы

Примечания

1. Разрезы — по линиям 1–1, 2–2 на плане потолков (лист 30). Отметки — от ±0,000 чистого пола, м; размеры — мм.
2. Высоты мебели и дверных блоков за секущей плоскостью сверены с низом потолка над ними: верх ниже низа короба и поля.
3. ГКЛ 12,5 мм по каркасу П113. Ниша под шторы — на всю длину стены с окном, карниз на закладной до обшивки (узел 1 — на этом листе).
4. Толщины плит перекрытия и пирога пола показаны условно.
5. Сечения потолков по помещениям М 1:10 (отметки помещения, профили, подвесы, крепёж, изделия) — лист 33.
6. Ведомость объёмов потолков (лист ГКЛ, профиль, подвесы, лента, блоки питания, люки) — на листе 32.

					Проект: Квартира 68 м², элитный модерн		М 1:40; 1:10
	Лист	№ док.	Подпись	Дата	Разрезы и узлы потолков	Стадия	Лист	Листов
Дизайнер	Кырлан А.С.			04.11.26		П	31	86

Ведомость объёмов потолков

Позиция	Ед.	Кол.	Пом.
Лист ГКЛ 12,5	м²	62,91	1, 4, 5, 6, 7
Лист ГКЛВ 12,5	м²	5,81	2, 3
Борта и карнизы (входят в площади листов выше)	м²	0,69	4, 5, 7
Профиль ПП 60×27	м	194,45	1, 2, 3, 4, 5, 6, 7
Профиль ПН 28×27	м	104,41	1, 2, 3, 4, 5, 6, 7
Подвес прямой	шт.	61	1, 2, 3, 4, 5, 6, 7
Анкер-клин к плите	шт.	61	1, 2, 3, 4, 5, 6, 7
Шуруп TN 3,5×25	шт.	1581	1, 2, 3, 4, 5, 6, 7
Лента армирующая для швов	м	82,46	1, 2, 3, 4, 5, 6, 7
Шпаклёвка для швов	кг	27,49	1, 2, 3, 4, 5, 6, 7
Грунтовка (швы)	л	6,87	1, 2, 3, 4, 5, 6, 7
Лента разделительная по периметру	м	87,03	1, 2, 3, 4, 5, 6, 7
Сплошная шпаклёвка и окраска (площадь развёртки)	м²	68,72	1, 2, 3, 4, 5, 6, 7

Примечания

1. ГКЛ 12,5 мм по каркасу П113; узлы коробов и ниш под шторы: узел 1 — лист 31; условные обозначения разрезов — на листе 31.
2. Ведомость объёмов — по геометрии плана потолков: Лист ГКЛ 12,5 — плоскости уровней + борта (без арочных участков); Лист ГКЛВ 12,5 — плоскости уровней + борта; Борта и карнизы — длина перепада × перепад; Профиль ПП 60×27 — S × (1/шаг несущ. + 1/шаг осн.) + стойки бортов; Профиль ПН 28×27 — периметр стен + 2 × перепады + карнизы; Подвес прямой — по раскладке: S уровня / (шаг осн. × шаг подвесов), пояс уже шага — ряд вдоль пояса, фигура — по контуру; шаг подвесов — не больше табл. 14 СП 163; Анкер-клин к плите — по одному на подвес (Knauf П113); Шуруп TN 3,5×25 — 23 шт./м² (Knauf П113, табл. 2 альбома П 11); Лента армирующая для швов — 1,2 м/м² листа (Knauf); Шпаклёвка для швов — 0,4 кг/м² листа, только швы (Knauf); Грунтовка (швы) — 0,1 л/м² листа, только швы (Knauf); Лента разделительная по периметру — периметр стен под потолком ГКЛ; Сплошная шпаклёвка и окраска (площадь развёртки) — плоскости + борта; расход — по паспорту материала (норма расхода на сплошной слой не подтверждена); без запаса на подрезку (при закупке листа: ×1,075 при S > 20 м², ×1,175 — 10–20 м², ×1,275 — < 10 м²).


					Проект: Квартира 68 м², элитный модерн
	Лист	№ док.	Подпись	Дата	
Дизайнер	Кырлан А.С.			04.11.26	Разрезы и узлы потолков (продолжение)

Стадия	Лист	Листов
П	32	86

Правка к этому листу

Сечение 5.1. Ниша под шторы (М 1:10)

Пом. 5 Кухня-столовая, 7 Спальня; без подсветки; закладные под карниз — до обшивки

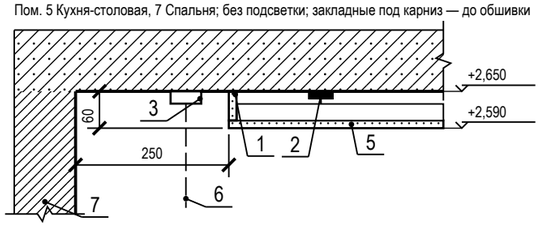

1 — стенка ниши — ГКЛ 12,5

2 — анкер-клин к плите — по одному на подвес; подвес прямой, шаг 1000 мм

3 — карниз (шина), высота с верхом портьеры 60 мм

4 — ПП 60×27 — каркас короба, основные через 1200 мм; соединители одноуровневые, шурупы LN 3,5×9


5 — низ короба нижнего уровня — ГКЛ 12,5; шурупы TN 3,5×25 через 170 мм

6 — портьера

7 — стена с окном

Сечение 5.2. Примыкание потолка к стене (М 1:10)

Пом. 5 Кухня-столовая, 7 Спальня; примыкание — теневой шов

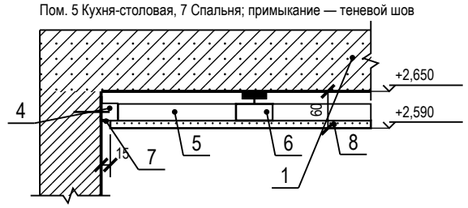

1 — плита перекрытия

2 — анкер-клин к плите — по одному на подвес

3 — подвес прямой, шаг 1000 мм

4 — ПН 28×27 по периметру — дюбель-гвоздь через ≤ 500 мм, не менее 3 на профиль

5 — ПП 60×27 несущий (вид) через 500 мм, в ПН

6 — ПП 60×27 основной (сечение) через 1200 мм; соединители одноуровневые, шурупы LN 3,5×9

7 — теневой профиль: шов 15 мм, зазор 3 мм; стена под шов выровнена

8 — ГКЛ 12,5 по П113; шурупы TN 3,5×25 через 170 мм


Примечания

1. Сечения потолков М 1:10 по помещениям с нишами LED и нишами под шторы: отметки и размеры этого помещения от ±0,000 чистого пола (м, мм). Положение — по плану потолков (лист 30): короб и ниша LED — по линиям ленты, ниша под шторы — у стены с окном; типовые узлы по группам помещений — на листе 31.
2. Крепёж: подвес прямой к плите на анкер-клине — по одному на подвес (Knauf П113); ПН к стенам — дюбель-гвоздь через ≤ 500 мм, не менее 3 на профиль (серия 1.045.9-2.08); лист 12,5 — шурупы TN 3,5×25 через 170 мм (СП 163, табл. 15); профили между собой — соединители одноуровневые, шурупы LN 3,5×9.
3. Изделие карниза, профиля LED и галтели подписано артикулом из данных; где артикул не выбран, сечение дано по габаритам из данных (ширина и глубина ниши, щель под свет), изделие подбирается по ним.

					Проект: Квартира 68 м², элитный модерн	**М 1:10**
	Лист	№ док.	Подпись	Дата		
Дизайнер	Кырлан А.С.			04.11.26	Сечения потолков М 1:10	Стадия: П; Лист: 33; Листов: 86

выпуск 04.11.2026 № f0db2de63c · стр. 33 из 86

Правка к этому листу

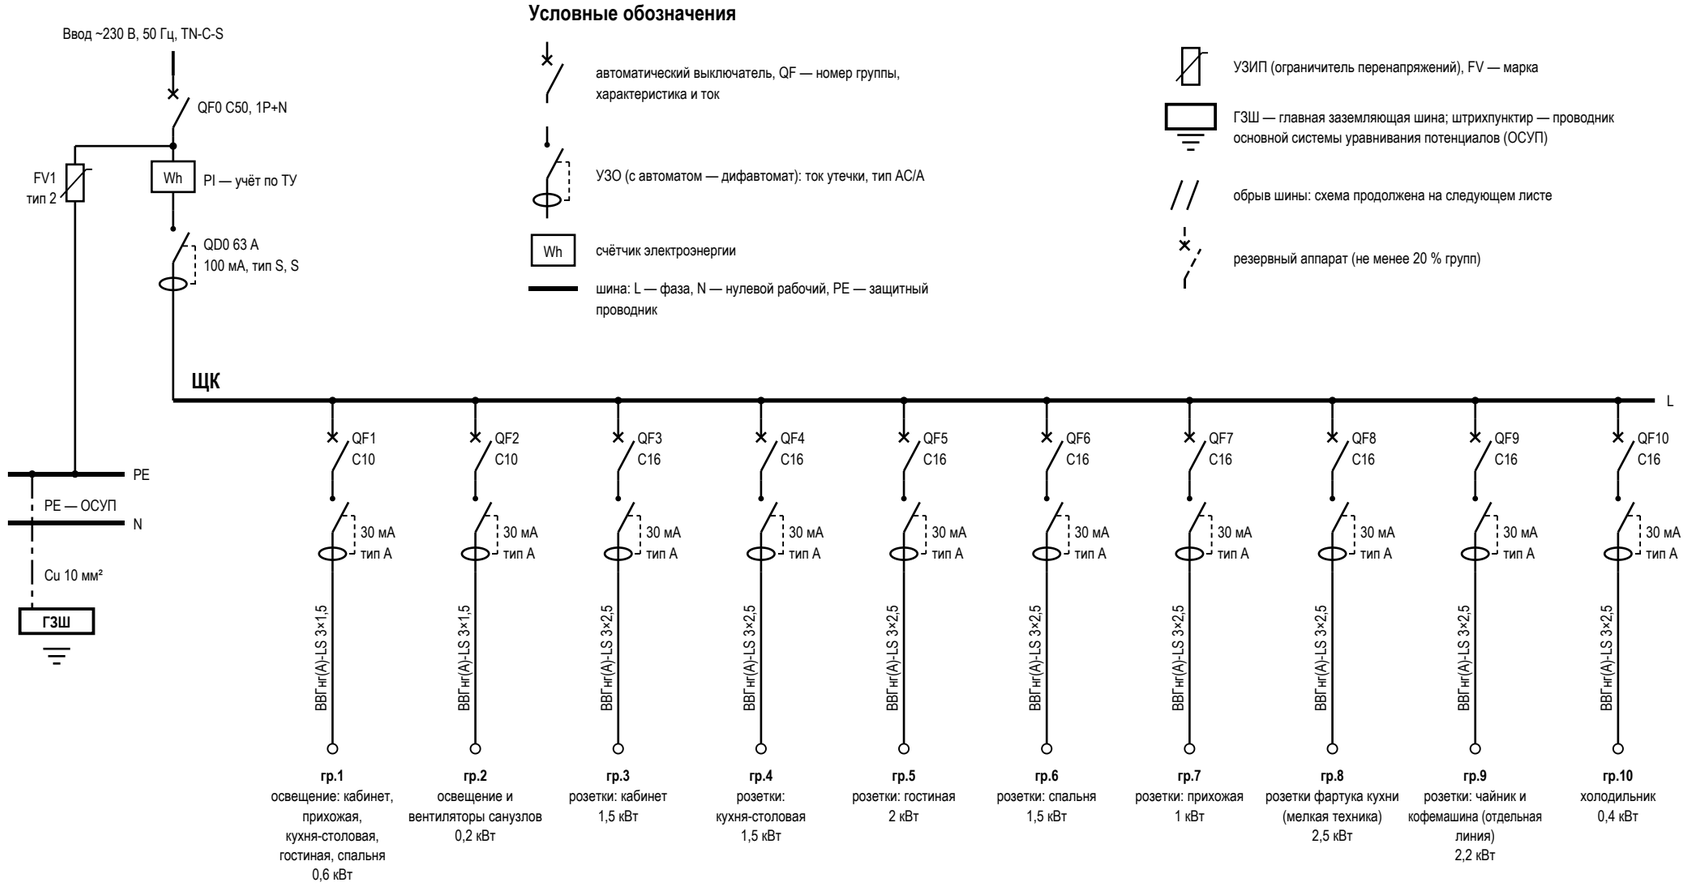

Условные обозначения

- автоматический выключатель, QF — номер группы, характеристика и ток
- УЗО (с автоматом — дифавтомат): ток утечки, тип AC/A
- Wh — счётчик электроэнергии
- шина: L — фаза, N — нулевой рабочий, PE — защитный проводник
- УЗИП (ограничитель перенапряжений), FV — марка
- ГЗШ — главная заземляющая шина; штрихпунктир — проводник основной системы уравнивания потенциалов (ОСУП)
- обрыв шины: схема продолжена на следующем листе
- резервный аппарат (не менее 20 % групп)

Данные щитка

Показатель	Значение
Номер щитка	ЩК
Тип	ЩРВ-П-72, IP41
Уст. мощность, кВт	33,1
Разреш. мощность, кВт	10
Расчётная, кВт	10,8
Расчётная > разрешённой	10,8 > 10 кВт: превышение 0,8 кВт
Автоматы 1п: занят. / рез.	20 / 4
Модулей: всего / занято	72 / 46
Ток на вводе, А	50
Вводной аппарат	QF0 C50, 1P+N
УЗИП	FV1, тип 2, ЩК, после счётчика
ГЗШ, проводник ОСУП	Cu 10 мм²
Листов схемы	2 (группы по листам)

Таблица групп щита ЩК и кабельный журнал

№	Назначение	Помещения	Автомат	УЗО / дифавтомат	Кабель	Длина, м	P, кВт	Точек
1	освещение: кабинет, прихожая, кухня-столовая, гостиная, спальня	1, 4, 5, 6, 7	C10	30 мА, тип A	ВВГнг(A)-LS 3×1,5	85	0,6	48
2	освещение и вентиляторы санузлов	2, 3, 4	C10	30 мА, тип A	ВВГнг(A)-LS 3×1,5	36	0,2	11
3	розетки: кабинет	1	C16	30 мА, тип A	ВВГнг(A)-LS 3×2,5	41	1,5	9
4	розетки: кухня-столовая	5	C16	30 мА, тип A	ВВГнг(A)-LS 3×2,5	41	1,5	1
5	розетки: гостиная	6	C16	30 мА, тип A	ВВГнг(A)-LS 3×2,5	41	2	10
6	розетки: спальня	7	C16	30 мА, тип A	ВВГнг(A)-LS 3×2,5	41	1,5	11
7	розетки: прихожая	4	C16	30 мА, тип A	ВВГнг(A)-LS 3×2,5	30	1	1
8	розетки фартука кухни (мелкая техника)	5	C16	30 мА, тип A	ВВГнг(A)-LS 3×2,5	18	2,5	6
9	розетки: чайник и кофемашина (отдельная линия)	5	C16	30 мА, тип A	ВВГнг(A)-LS 3×2,5	18	2,2	1
10	холодильник	5	C16	30 мА, тип A	ВВГнг(A)-LS 3×2,5	18	0,4	1

Примечания

1. Схема однолинейная: одна линия — фаза, N и PE группы; аппараты — в отключённом положении (ГОСТ 2.702, ГОСТ 2.755). Номера групп — как у точек на планах (гр.). За отметку 0,000 принят уровень чистого пола; высота щита — по плану розеток.
2. Розеточные и мокрые линии — через УЗО или дифавтомат с током утечки не более 30 мА (ПУЭ 7.1.79); в санузле выполнить ДСУП (ПУЭ 7.1.87–7.1.88).
3. УЗО тип A — для линий с электроникой, стиральной и посудомоечной машиной, LED-драйверами; тип AC — только для чисто активной нагрузки.
4. Кабель — медный, исполнение нг(A)-LS (ГОСТ 31565-2012); скрытая прокладка только горизонтально и вертикально, фактические трассы зафиксировать исполнительной схемой до закрытия отделкой.
5. Номинал автомата — не выше допустимого тока кабеля: 1,5 мм² — до 10 А, 2,5 мм² — до 16 А. Резерв щита — не менее 20 % модулей.
6. Расчёт нагрузок, токов КЗ, селективности и сечений — по проекту ЭОМ организации с допуском СРО; лист задаёт состав, расположение и группы.
7. УЗИП FV1 — после вводного автомата, проводник к шине PE — кратчайший, без петель. Шина PE щита соединяется с ГЗШ проводником ОСУП; к ГЗШ присоединяются трубы водопровода и отопления на вводе в квартиру (ПУЭ 7.1.87). Шины N и PE — раздельные, после разделения PEN не объединяются.
8. До подключения нагрузки — приёмо-сдаточные испытания с протоколом: сопротивление изоляции линий не менее 0,5 МОм, срабатывание УЗО по току и времени, непрерывность защитных проводников PE (ПУЭ, гл. 1.8).

					Проект: Квартира 68 м², элитный модерн
	Лист	№ док.	Подпись	Дата	
Дизайнер	Кырлан А.С.			04.11.26	Однолинейная схема щита
					Стадия: П; Лист: 34; Листов: 86

Продолжение однолинейной схемы щита ЩК, начало — лист 34

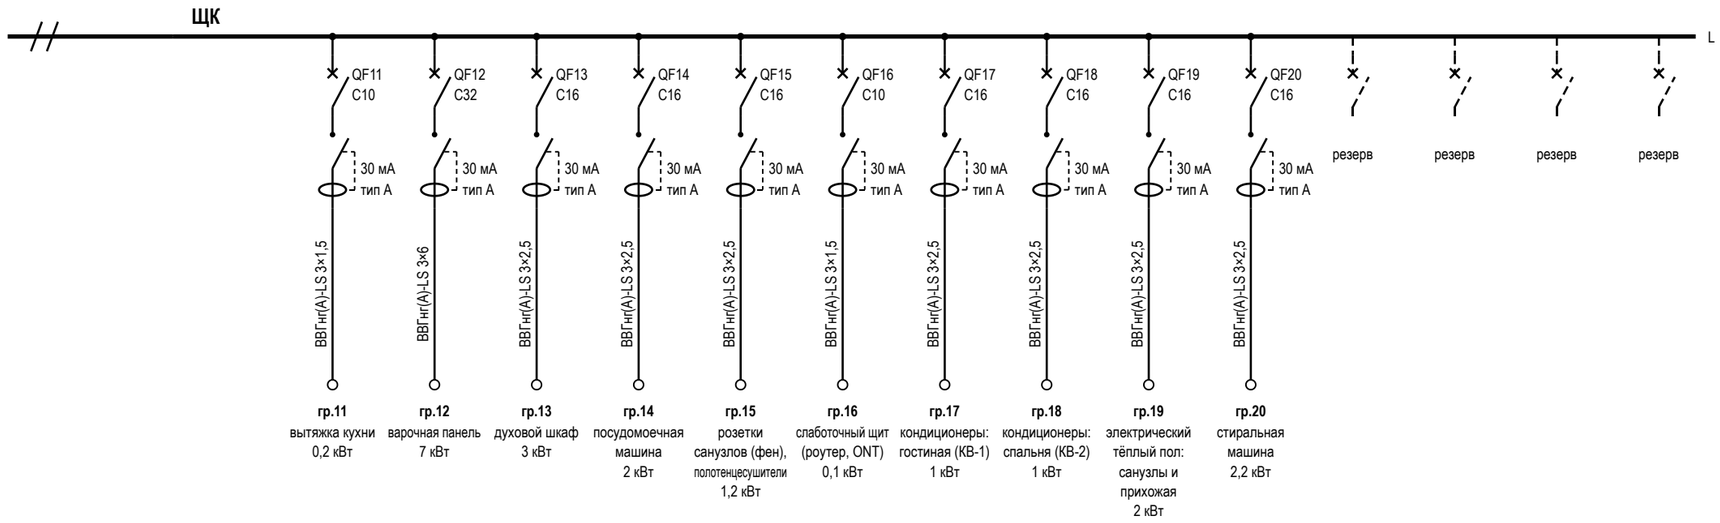



Таблица групп щита ЩК и кабельный журнал (продолжение)

№	Назначение	Помещения	Автомат	УЗО / дифавтомат	Кабель	Длина, м	Р, кВт	Точек
11	вытяжка кухни	5	C10	30 мА, тип A	ВВГнг(A)-LS 3×1,5	18	0,2	1
12	варочная панель	5	C32	30 мА, тип A	ВВГнг(A)-LS 3×6	18	7	1
13	духовой шкаф	5	C16	30 мА, тип A	ВВГнг(A)-LS 3×2,5	18	3	1
14	посудомоечная машина	5	C16	30 мА, тип A	ВВГнг(A)-LS 3×2,5	18	2	1
15	розетки санузлов (фен), полотенцесушители	2, 3	C16	30 мА, тип A	ВВГнг(A)-LS 3×2,5	27	1,2	2
16	слаботочный щит (роутер, ONT)	4	C10	30 мА, тип A	ВВГнг(A)-LS 3×1,5	6	0,1	6
17	кондиционеры: гостиная (КВ-1)	6	C16	30 мА, тип A	ВВГнг(A)-LS 3×2,5	41	1	1
18	кондиционеры: спальня (КВ-2)	7	C16	30 мА, тип A	ВВГнг(A)-LS 3×2,5	41	1	1
19	электрический тёплый пол: санузлы и прихожая	3, 4	C16	30 мА, тип A	ВВГнг(A)-LS 3×2,5	18,8	2	2
20	стиральная машина	3	C16	30 мА, тип A	ВВГнг(A)-LS 3×2,5	15	2,2	1
	Итого по сечениям ВВГнг(A)-LS (все группы щита), м: 3×1,5 — 145; 3×2,5 — 426,8; 3×6 — 18					589,8		

Примечания

1. Лист — продолжение однолинейной схемы щита ЩК: начало, данные щитка и условные обозначения — лист 34. Ввод, учёт, вводной аппарат, УЗИП, шины N и PE и ГЗШ показаны там же; шина L листа — та же шина щита.
2. Схема однолинейная: одна линия — фаза, N и PE группы; аппараты — в отключённом положении (ГОСТ 2.702, ГОСТ 2.755). Номера групп — как у точек на планах (гр.). За отметку 0,000 принят уровень чистого пола; высота щита — по плану розеток.
3. Розеточные и мокрые линии — через УЗО или дифавтомат с током утечки не более 30 мА (ПУЭ 7.1.79); в санузле выполнить ДСУП (ПУЭ 7.1.87–7.1.88).
4. УЗО тип A — для линий с электроникой, стиральной и посудомоечной машиной, LED-драйверами; тип AC — только для чисто активной нагрузки.
5. Кабель — медный, исполнение нг(A)-LS (ГОСТ 31565-2012); скрытая прокладка только горизонтально и вертикально, фактические трассы зафиксировать исполнительной схемой до закрытия отделкой.
6. Номинал автомата — не выше допустимого тока кабеля: 1,5 мм² — до 10 А, 2,5 мм² — до 16 А. Резерв щита — не менее 20 % модулей.
7. Расчёт нагрузок, токов КЗ, селективности и сечений — по проекту ЭОМ организации с допуском СРО; лист задаёт состав, расположение и группы.
8. До подключения нагрузки — приёмо-сдаточные испытания с протоколом: сопротивление изоляции линий не менее 0,5 МОм, срабатывание УЗО по току и времени, непрерывность защитных проводников PE (ПУЭ, гл. 1.8).

					Проект: Квартира 68 м², элитный модерн
	Лист	№ док.	Подпись	Дата	
Дизайнер	Кырлан А.С.			04.11.26	Однолинейная схема щита (продолжение)
					Стадия: П; Лист: 35; Листов: 86

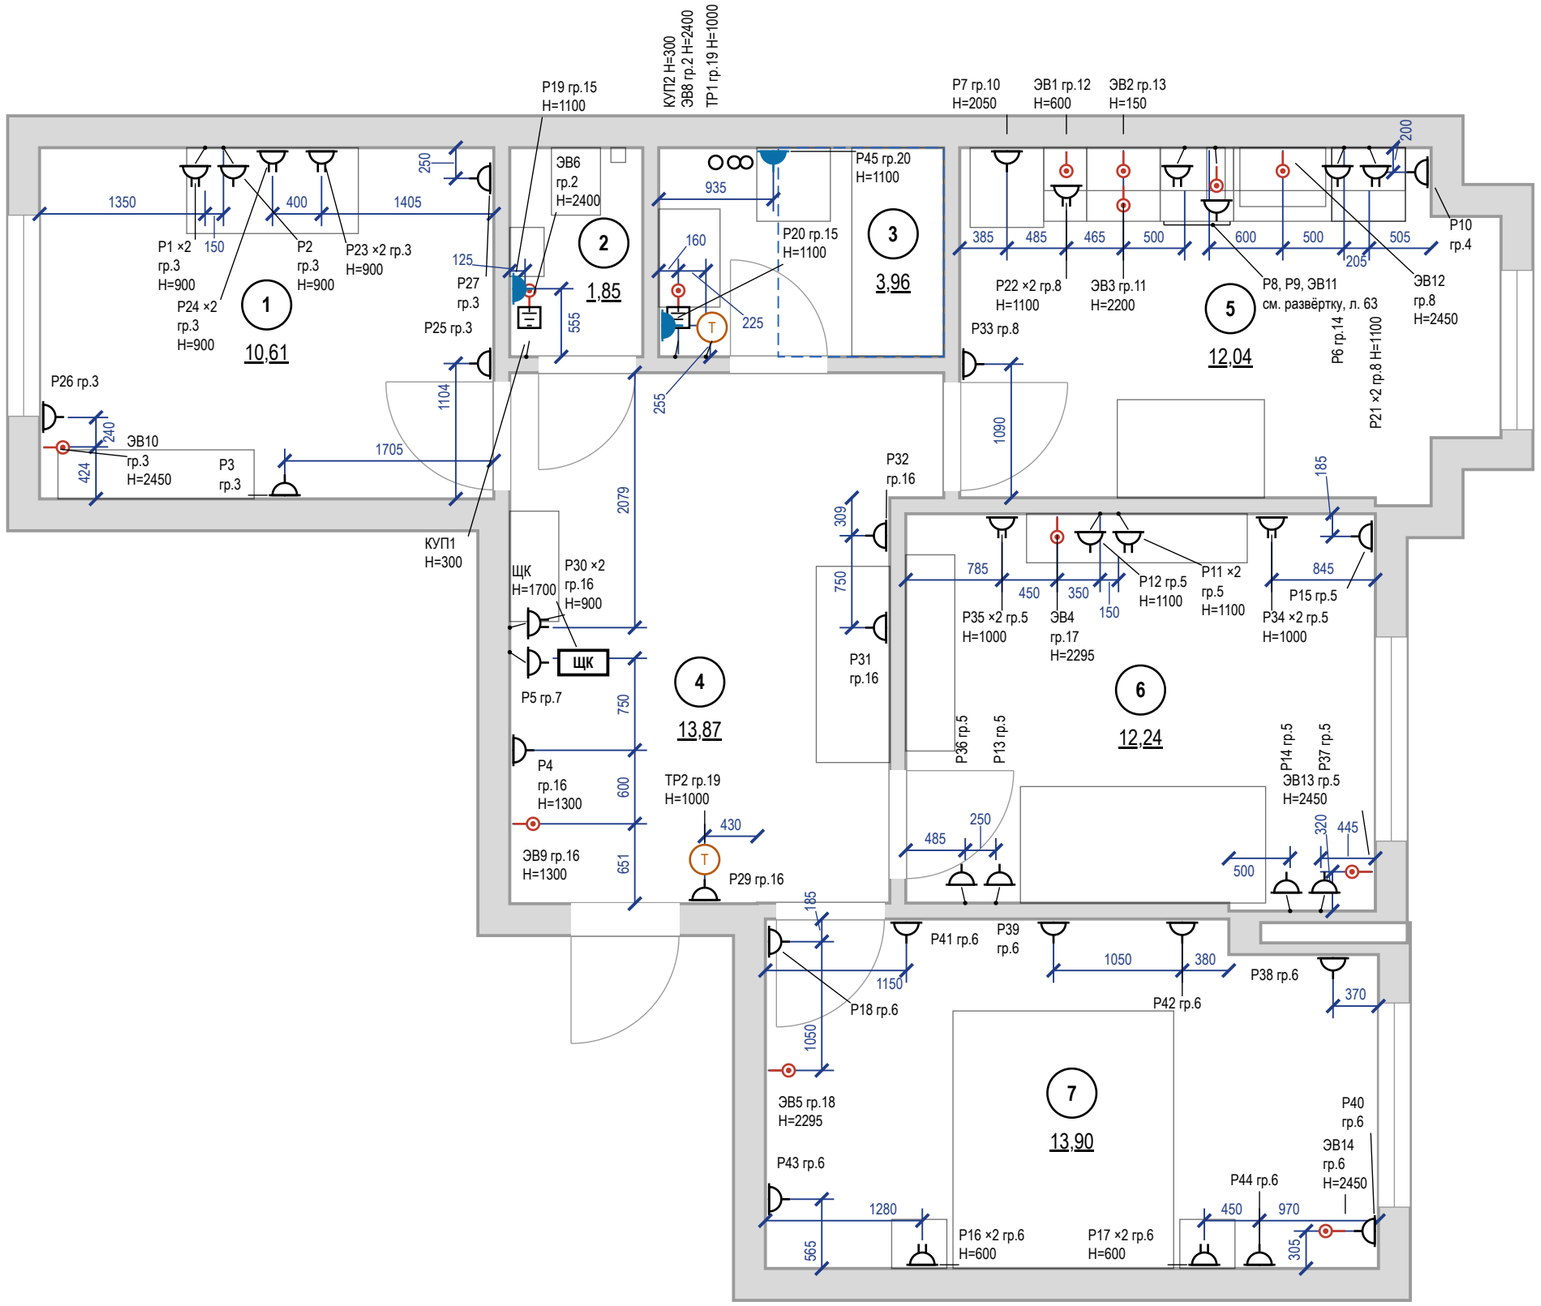

Условные обозначения

Знак	Тип изделия	H, мм	Кол., шт
	Розетка с заземлением	300	24
	То же	у знака	5
	Блок розеток с заземлением, рамка 2 поста	у знака	12
	Розетка с заземлением IP44	1100	3
	Вывод кабеля к прибору	у знака	13
	КУП (уравнивание потенциалов)	300	2
T	Терморегулятор тёплого пола	1000	2
ЩК	Щит квартирный	1700	1

розетка с заземляющим контактом; у знака — марка, ×N — постов в рамке, гр. — группа щита, H — высота оси, мм

знак разведён для читаемости: точка на стене — у выноски, привязка — до неё

граница зоны 2 ванной (600 мм от ванны/поддона)

мебель и сантехприборы — подложка

стояк: К1 — канализация, В1 — ХВС, Т3 — ГВС


1 — номер помещения, площадь м²

Итого розеток (механизмов) — 56 шт; рамок — 44 шт: на 1 пост — 32, на 2 поста — 12.

Примечания

1. За отметку 0,000 принят уровень чистого пола. Высоты H — от чистого пола до оси изделия; привязки — от чистовой грани стены до оси механизма (у рамки на несколько постов — до оси рамки).
2. Розетки без отметки H у знака — на высоте 300 мм от чистого пола до оси механизма; выводы кабеля — по паспорту прибора.
3. Розетки в санузле — только вне зон 0–2 (ПУЭ 7.1.48, ГОСТ Р 50571.7.701-2024), IP44, через УЗО 30 мА.
4. Розеточные и мокрые линии — через УЗО или дифавтомат с током утечки не более 30 мА (ПУЭ 7.1.79); в санузле выполнить ДСУП (ПУЭ 7.1.87–7.1.88).
5. Кабель — медный, исполнение нг(A)-LS (ГОСТ 31565-2012); скрытая прокладка только горизонтально и вертикально, фактические трассы зафиксировать исполнительной схемой до закрытия отделкой.
6. Расчёт нагрузок, токов КЗ, селективности и сечений — по проекту ЭОМ организации с допуском СРО; лист задаёт состав, расположение и группы.
7. Выводы кухонной техники — после утверждения проекта кухни (ориентировочно); привязки выводов даны от осей модулей гарнитура и пересматриваются вместе с проектом кухни.

					Проект: Квартира 68 м², элитный модерн — **М 1:50**
	Лист	№ док.	Подпись	Дата	План розеток и электровыводов
Дизайнер	Кырлан А.С.			04.11.26	Стадия: П; Лист: 36; Листов: 86

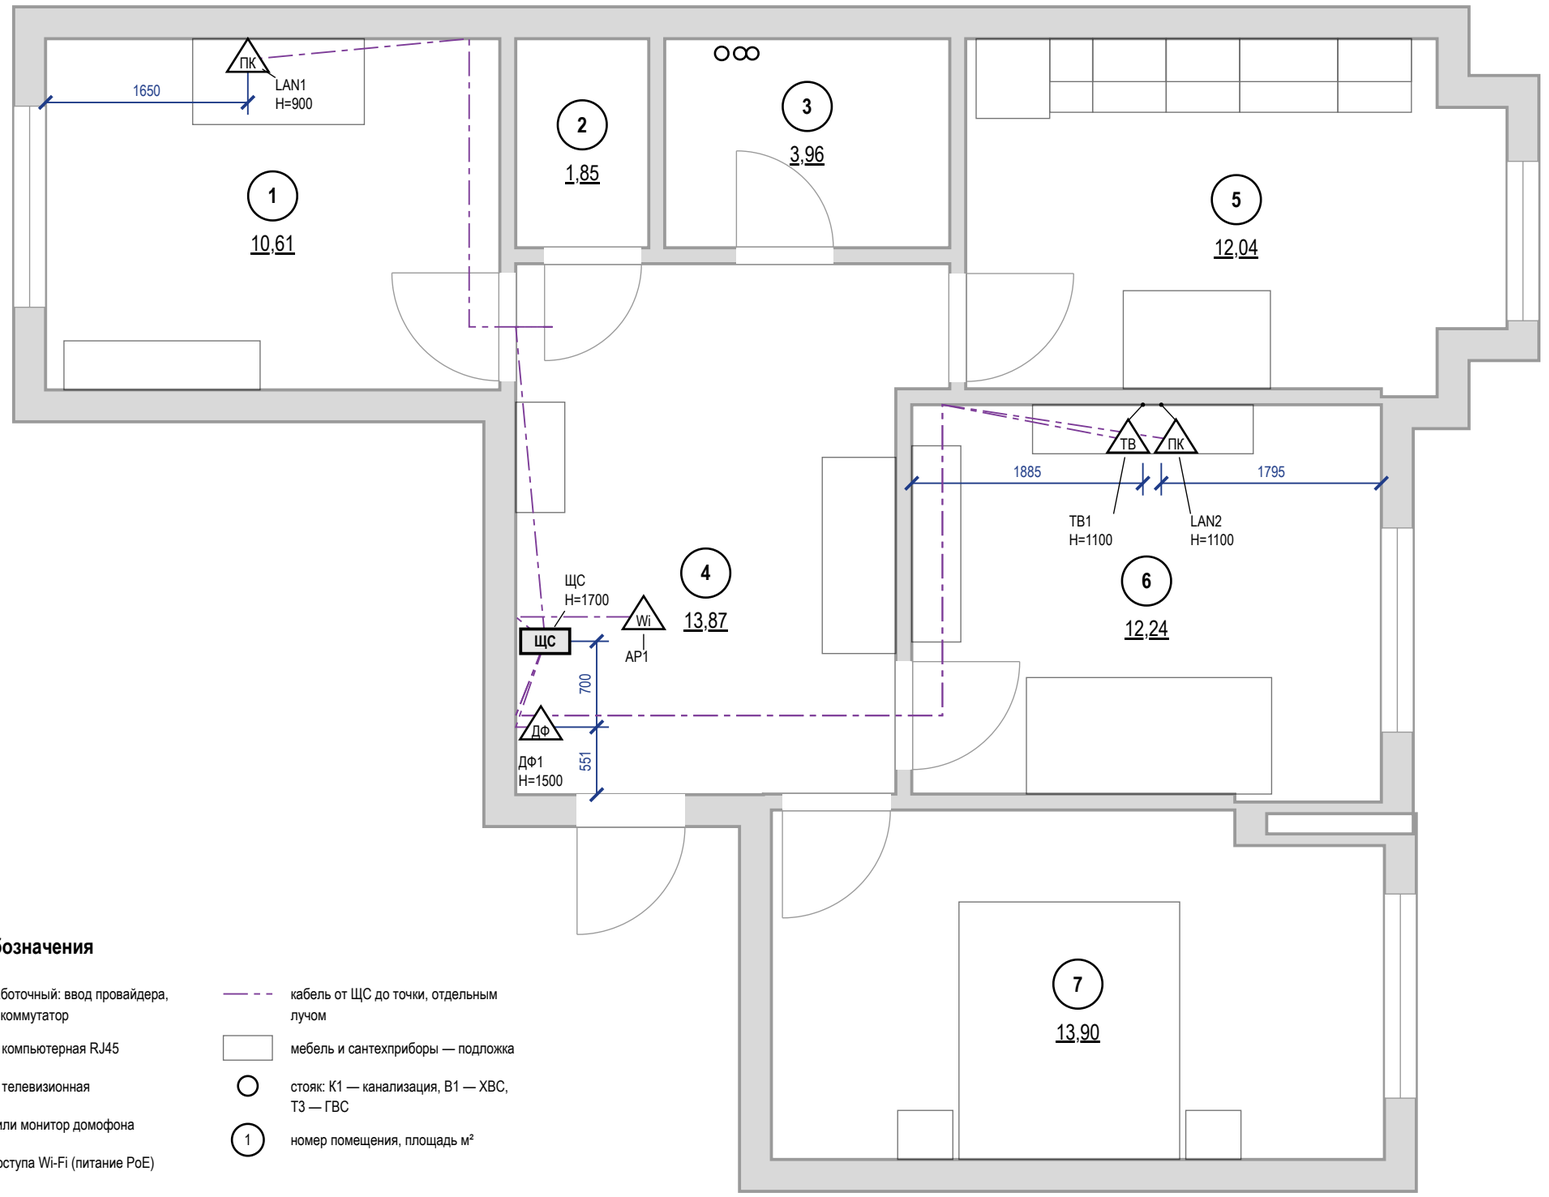


Условные обозначения

ЩС	щит слаботочный: ввод провайдера, роутер, коммутатор
ПК	розетка компьютерная RJ45
ТВ	розетка телевизионная
ДФ	трубка или монитор домофона
Wi	точка доступа Wi-Fi (питание PoE)
— — —	кабель от ЩС до точки, отдельным лучом
▭	мебель и сантехприборы — подложка
○	стояк: К1 — канализация, В1 — ХВС, Т3 — ГВС
1	номер помещения, площадь м²

Примечания

1. За отметку 0,000 принят уровень чистого пола. Высоты Н — от чистого пола до оси изделия; привязки — от чистовой грани стены до оси механизма (у рамки на несколько постов — до оси рамки).
2. Высота установки, не указанная на плане: розетки LAN и ТВ — 300 мм от чистого пола.
3. Слаботочные кабели — отдельно от силовых: в своей трубе или лотке, при параллельной прокладке не ближе 100 мм к силовым, пересечения под прямым углом; каждую точку — отдельным кабелем от ЩС без скруток.
4. Трассы на листе — принципиальные; фактические зафиксировать исполнительной схемой до закрытия отделкой. Силовые линии, УЗО 30 мА, ДСУП, кабель нг(А)-LS — по листам розеток и щита.
5. Проект силовой части и расчёт токов КЗ — по проекту ЭОМ; слаботочная часть согласуется с провайдером и управляющей компанией (домофон, коллективное ТВ).

					Проект: Квартира 68 м², элитный модерн — М 1:50
	Лист	№ док.	Подпись	Дата	
Дизайнер	Кырлан А.С.			04.11.26	План слаботочных сетей
					Стадия: П; Лист: 37; Листов: 86

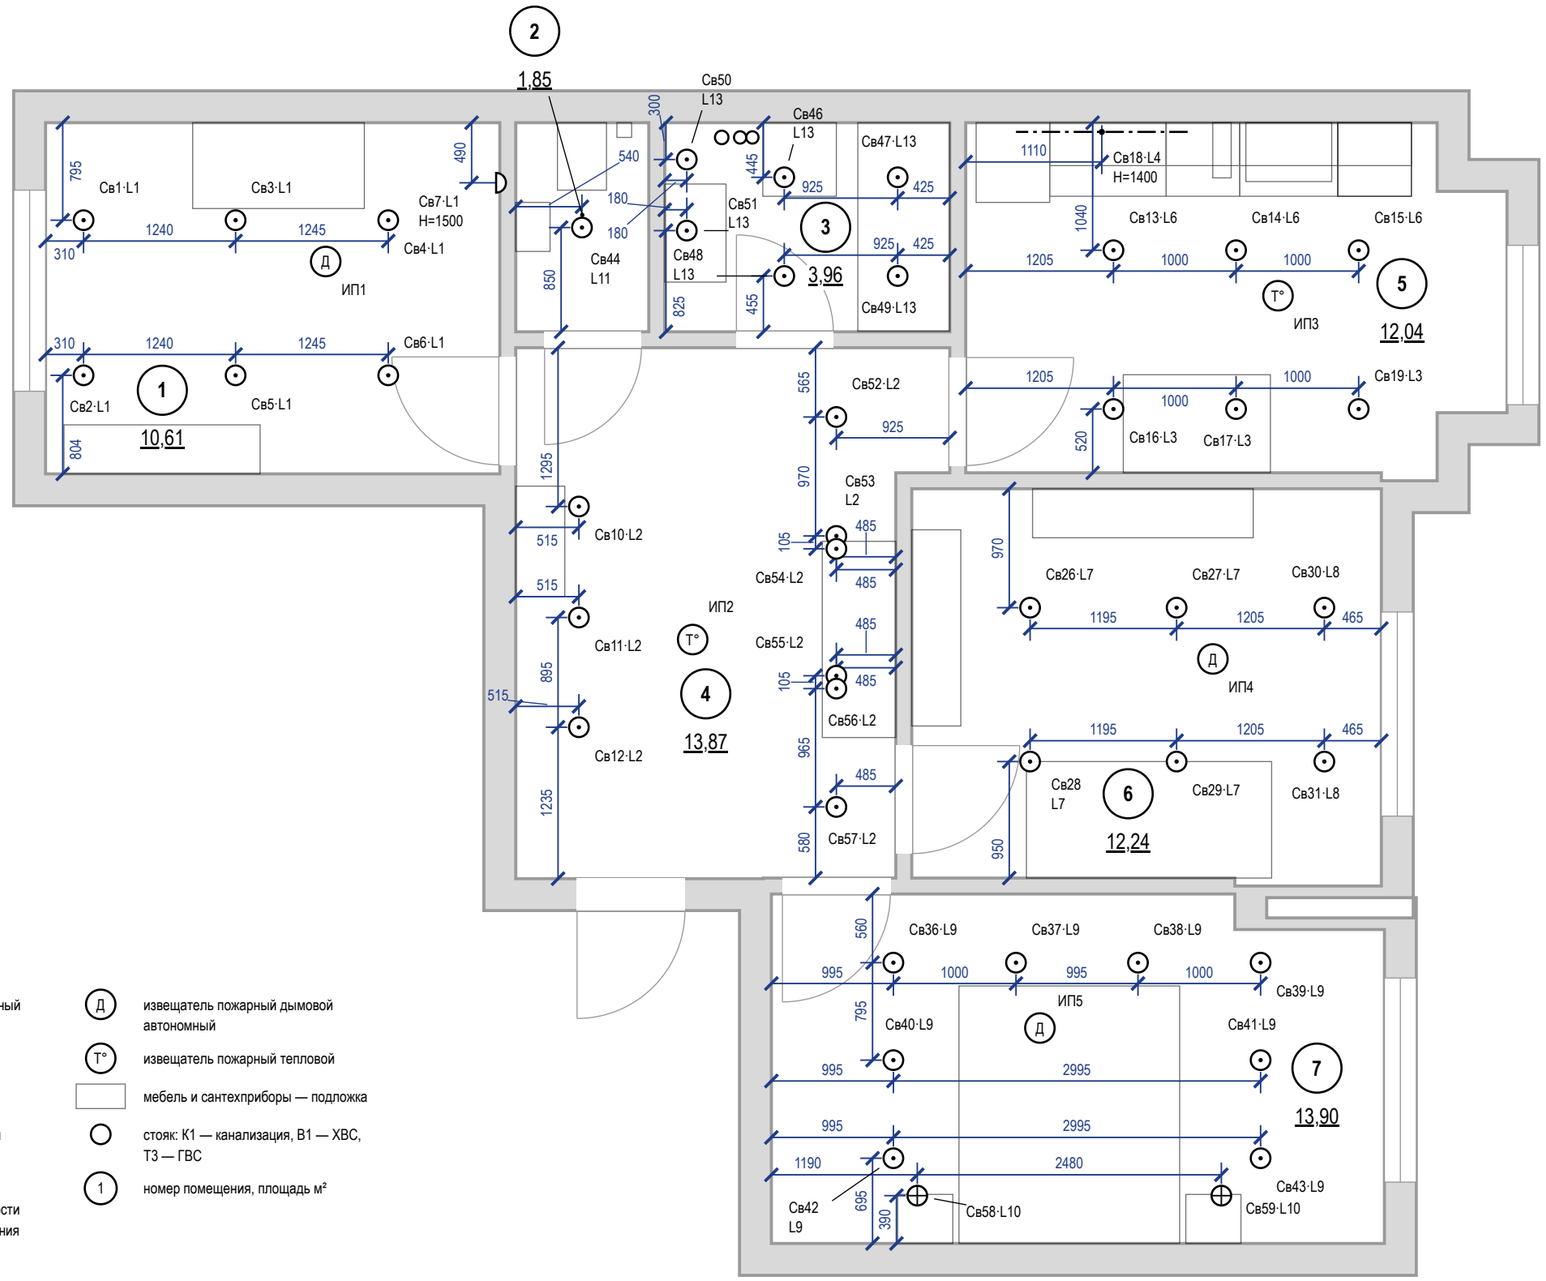

Условные обозначения

- светильник встраиваемый точечный
- светильник подвесной
- светильник настенный (бра), H высота оси
- линейный светильник настенный (подсветка столешницы), точка вывод питания
- Св1·L1 — марка светильника (как в ведомости и на развёртках) · группа включения L (лист 40)
- Д — извещатель пожарный дымовой автономный
- Т° — извещатель пожарный тепловой
- мебель и сантехприборы — подложка
- стояк: К1 — канализация, В1 — ХВС, Т3 — ГВС
- 1 — номер помещения, площадь м²

Примечания

1. За отметку 0,000 принят уровень чистого пола. Высоты H — от чистого пола до оси изделия; привязки — от чистовой грани стены до оси механизма (у рамки на несколько постов — до оси рамки).
2. Высота установки, не указанная на плане: светильники — на потолке; настенные — по отметке H у знака. Привязки — до оси светильника от чистовой грани стены, по рядам.
3. Во влажных помещениях — светильники не ниже IP44; в зонах 0–2 ванной — по ГОСТ Р 50571.7.701-2024 (зона 1 — IPX5).
4. Розеточные и мокрые линии — через УЗО или дифавтомат с током утечки не более 30 мА (ПУЭ 7.1.79); в санузле выполнить ДСУП (ПУЭ 7.1.87–7.1.88).
5. Кабель — медный, исполнение нг(A)-LS (ГОСТ 31565-2012); скрытая прокладка только горизонтально и вертикально, фактические трассы зафиксировать исполнительной схемой до закрытия отделкой.
6. Расчёт нагрузок, токов КЗ, селективности и сечений — по проекту ЭОМ организации с допуском СРО; лист задаёт состав, расположение и группы.
7. Ведомость светильников (тип, количество, мощность, поток, Tц, Ra) — лист 39.

					Проект: Квартира 68 м², элитный модерн	М 1:50
	Лист	№ док.	Подпись	Дата	План освещения	Стадия / Лист / Листов
Дизайнер	Кырлан А.С.			04.11.26		П / 38 / 86

Параметры светильников для подбора

Поз.	Марки	Наименование	Установка	Кол.	P, Вт	Σ P, Вт	Ф, лм	Тц, К	Ra	Угол, °	IP	Дим.	Слой	Группа	Пом.
1	Св1, Св2, Св3, Св4, Св5, Св6, Св10, Св11, Св12, Св13, Св14, Св15, Св16, Св17, Св19, Св26, Св27, Св28, Св29, Св30, Св31, Св36, Св37, Св38, Св39, Св40, Св41, Св42, Св43	Встраиваемый точечный, встраиваемый LED-светильник, монтажная глубина ≤ 50 мм аналог по характеристикам	в ГКЛ, корпус ≤ 50 мм	29	7	203	600	2700	90	—	20	—	общий	L1, L2, L3, L6, L7, L8, L9	1, 4, 5, 6, 7
2	Св7	Настенный (бра)	на стене, H=1500	1	5	5	300	2700	90	—	20	—	рабочий	L1	1
3	Св44, Св46, Св47, Св48, Св49, Св50, Св51	Встраиваемый точечный, встраиваемый LED-светильник IP44, монтажная глубина ≤ 50 мм — аналог по характеристикам	в ГКЛ, корпус ≤ 50 мм	7	7	49	600	2700	90	—	44	—	общий	L11, L13	2, 3
4	Св52, Св53, Св54, Св55, Св56, Св57	Встраиваемый точечный	в ГКЛ, корпус ≤ 50 мм	6	5	30	400	2700	90	24	20	—	акцентный	L2	4
5	Св18	Линейный настенный	под верхними шкафами, H=1400	1	30	30	2400	2700	90	—	20	—	рабочий	L4	5
6	Св58, Св59	Подвесной	подвес	2	6	12	400	2700	90	—	20	—	рабочий	L10	7
		Итого		**46 шт**		**329**									

LED-ленты, линейные светильники и блоки питания


Марка	Пом.	L, м	U, В	Вт/м	Σ P, Вт	БП	P БП, Вт	Загр., %	Питание	Доступ к БП
Св18	5	3	—	—	30	у ленты	36	83	встроенный ввод	люк ревизии 300×300 мм

Примечания

1. Позиции и марки Св — те же, что на плане освещения (лист 38); группы L — по плану выключателей (лист 40).
2. Модели выбраны не у всех позиций: лист — техническое задание на подбор. Модель по строке таблицы: поток, Тц, Ra, угол, IP и регулировка яркости не хуже указанных, мощность не больше; встраиваемые — под глубину короба (графа «Установка»). IP 20 — сухие помещения. После выбора моделей (артикул, производитель) лист выпускается как «Спецификация светильников».
3. Мощность и поток в таблице — требования к подбору (поток не меньше, мощность не больше указанных); после выбора модели — по её паспорту, Σ P — установленная мощность освещения. Оценка освещённости — на плане освещения; это не светотехнический расчёт.

					Проект: Квартира 68 м², элитный модерн
	Лист	№ док.	Подпись	Дата	
Дизайнер	Кырлан А.С.			04.11.26	Техническое задание на подбор светильников

Стадия	Лист	Листов
П	39	86

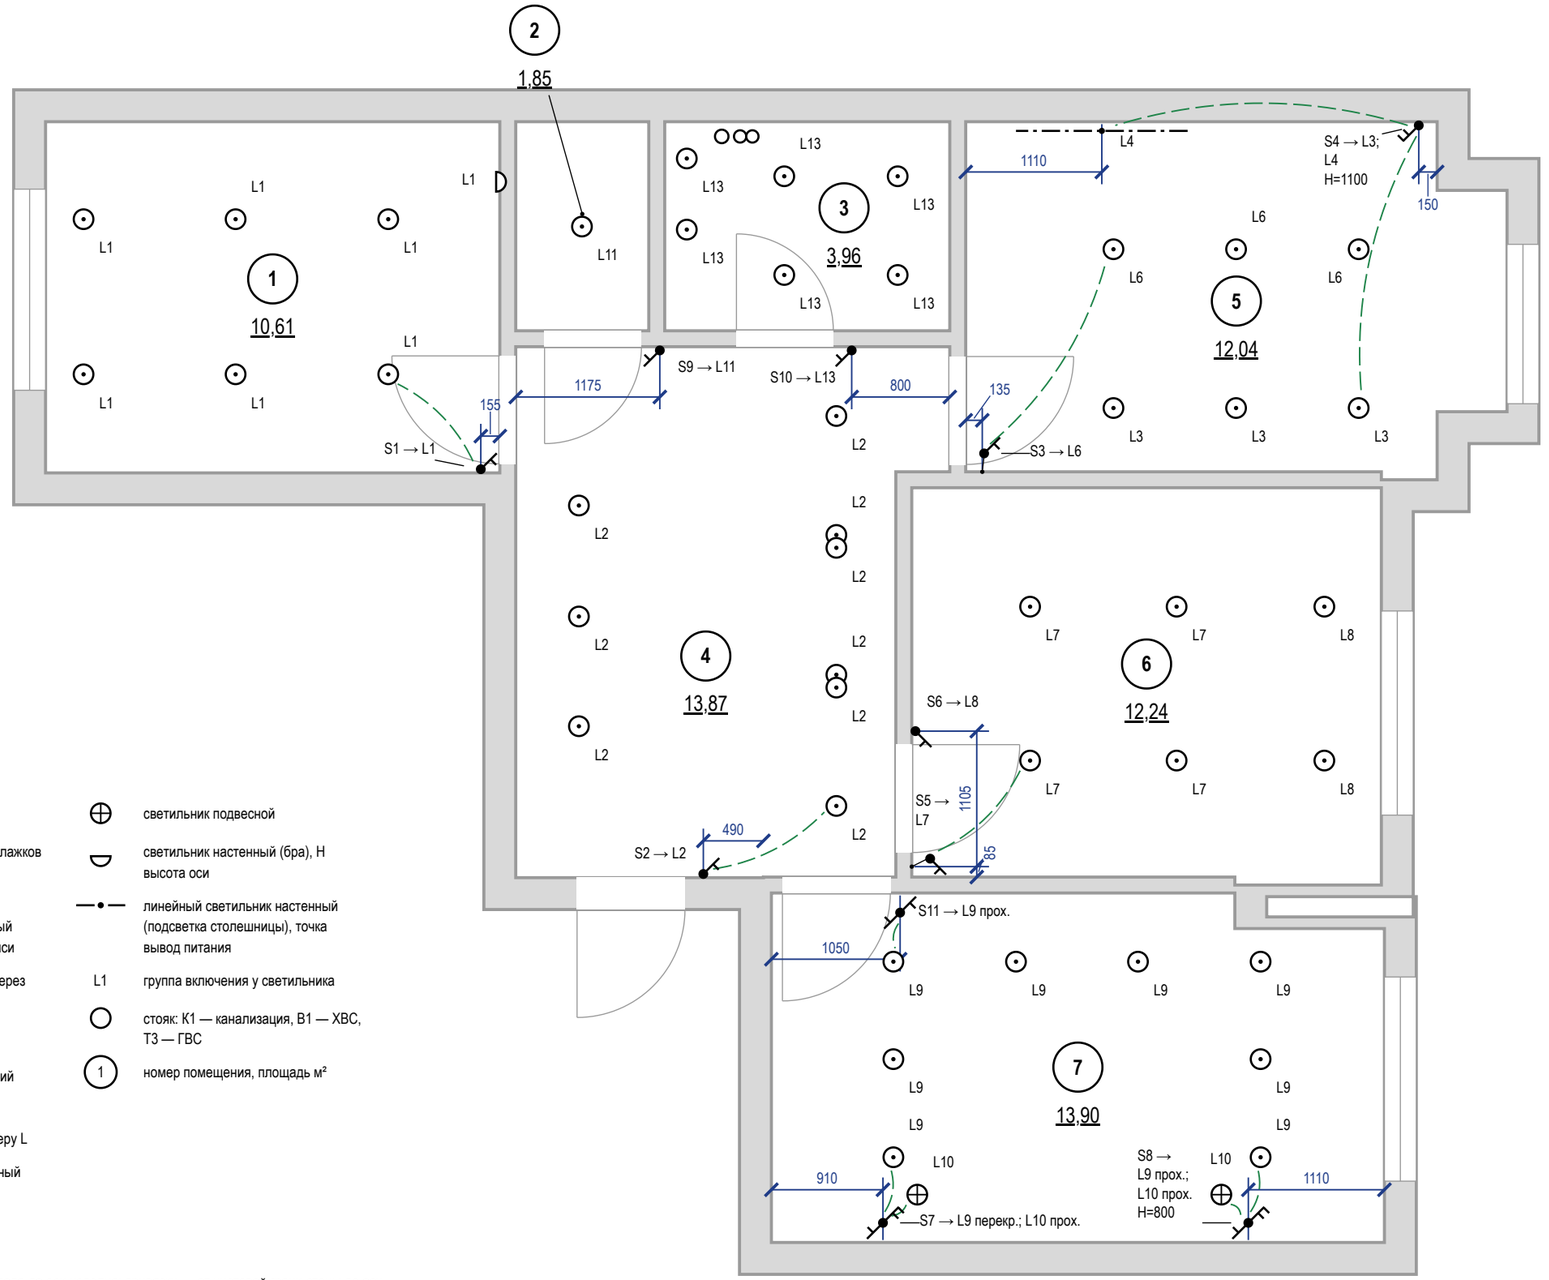


Условные обозначения

выключатель одноклавишный	светильник подвесной
выключатель двухклавишный (флажков — по числу клавиш)	светильник настенный (бра), H высота оси
выключатель с проходной или перекрёстной клавишей (обратный флажок); тип клавиши — в подписи	линейный светильник настенный (подсветка столешницы), точка вывод питания
S1 → марка → группы по клавишам (через «;»): прох. — проходной, перекр. перекрёстный, дим. светорегулятор; H — высота	L1 группа включения у светильника
связь: выключатель → ближайший светильник группы в том же помещении (не трасса кабеля); полный состав группы — по номеру L	стояк: К1 — канализация, В1 — ХВС, Т3 — ГВС
светильник встраиваемый точечный	1 номер помещения, площадь м²

Примечания

1. За отметку 0,000 принят уровень чистого пола. Высоты H — от чистого пола до оси изделия; привязки — от чистовой грани стены до оси механизма (у рамки на несколько постов — до оси рамки).
2. Высота установки, не указанная на плане: выключатели — 900 мм от чистого пола (у кровати и другие — H у марки), со стороны дверной ручки (ПУЭ 7.1.51).
3. Какой выключатель какие светильники включает — по номеру группы L: у выключателя (S1 → L1; L2 — клавиши по порядку) и у каждого светильника. Пунктир — подсказка к ближайшему светильнику группы в том же помещении (не дальше 3 м), это не трасса кабеля; выключатель за стеной (у двери санузла) и далёкая группа — только номер группы.
4. Группы из нескольких мест (L9 — S7, S8, S11; L10 — S7, S8): на крайних местах — проходные клавиши, на промежуточных — перекрёстные; механизмы — в ведомости изделий.
5. Розеточные и мокрые линии — через УЗО или дифавтомат с током утечки не более 30 мА (ПУЭ 7.1.79); в санузле выполнить ДСУП (ПУЭ 7.1.87–7.1.88).
6. Кабель — медный, исполнение нг(A)-LS (ГОСТ 31565-2012); скрытая прокладка только горизонтально и вертикально, фактические трассы зафиксировать исполнительной схемой до закрытия отделкой.
7. Расчёт нагрузок, токов КЗ, селективности и сечений — по проекту ЭОМ организации с допуском СРО; лист задаёт состав, расположение и группы.

					Проект: Квартира 68 м², элитный модерн — М 1:50
	Лист	№ док.	Подпись	Дата	Управление светильниками — Стадия: П; Лист: 40; Листов: 86
Дизайнер	Кырлан А.С.			04.11.26	

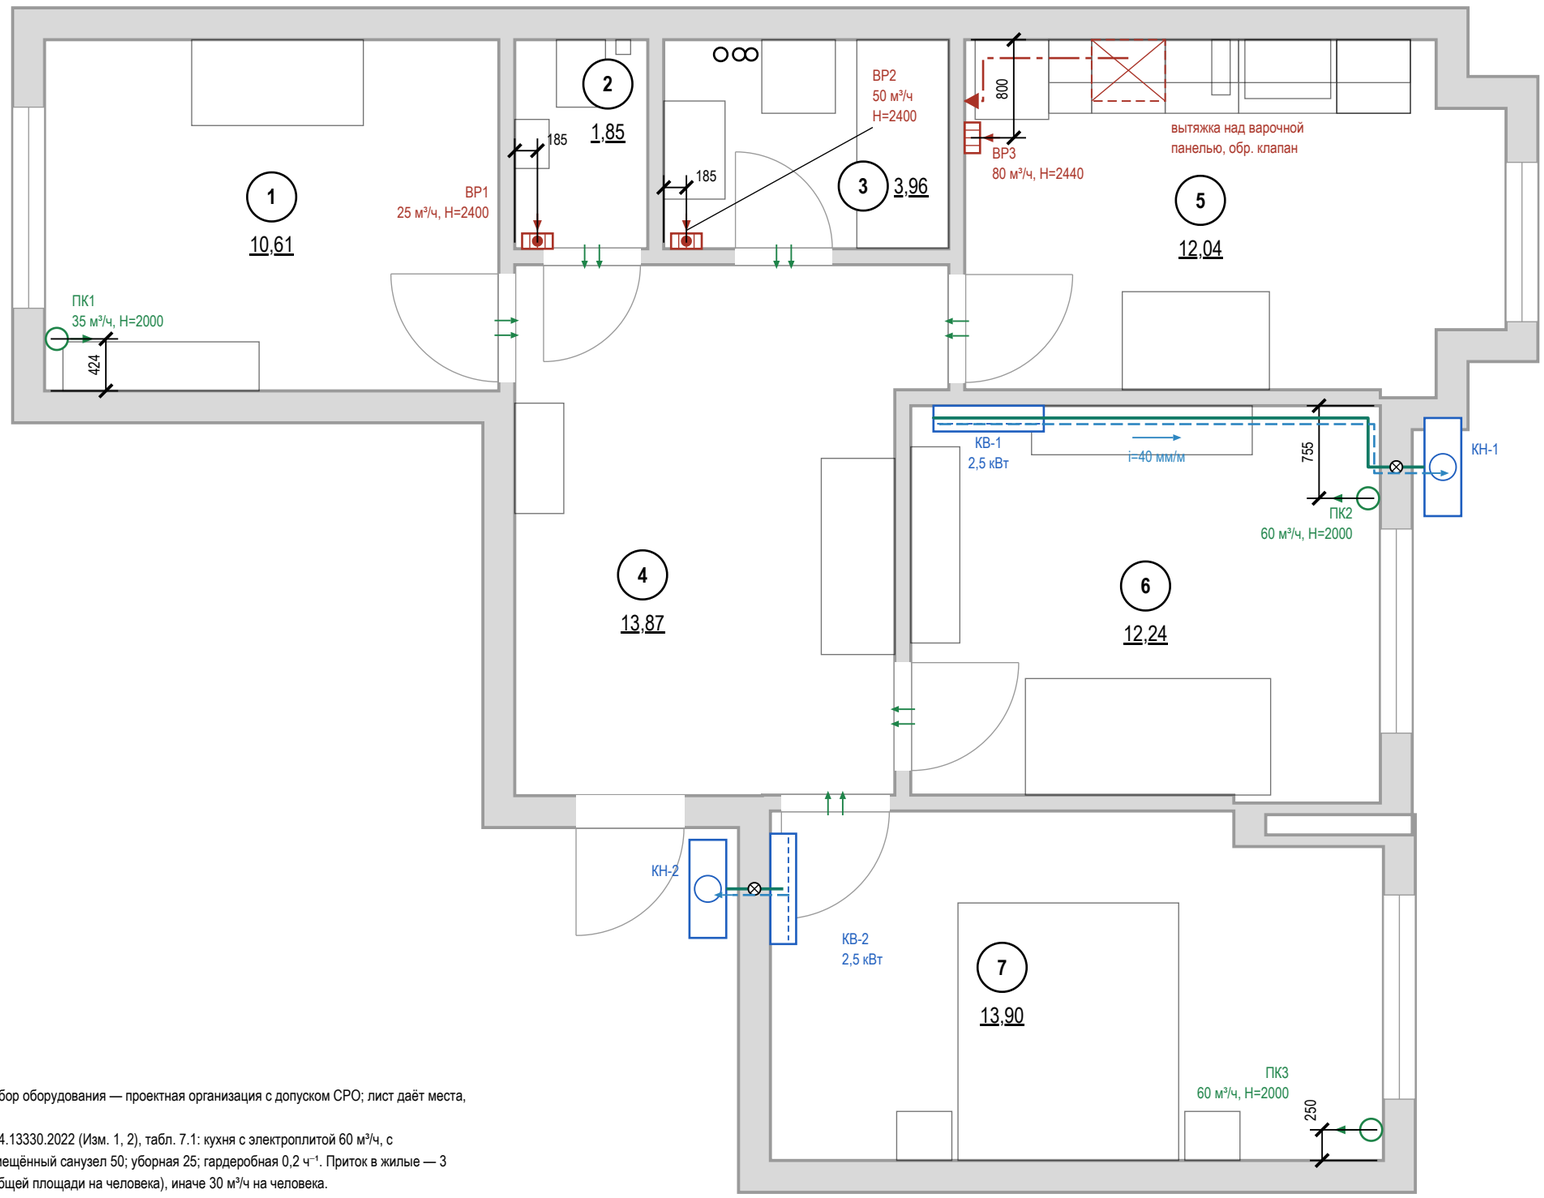

Условные обозначения

- стояк: К1 — канализация, В1 — ХВС, Т3 — ГВС
- номер помещения, площадь м²
- вытяжная решётка в вентканал: марка, расход м³/ч, H центра от чистого пола
- вытяжная решётка с бытовым вентилятором и обратным клапаном: марка, расход, H
- приточный клапан (КИВ) в наружной стене: марка, расход, H центра
- переток: зазор под полотном или переточная решётка
- кухонная вытяжка над варочной панелью
- воздуховод кухонной вытяжки в коробе под потолком
- отдельный вход воздуховода в вентканал, обратный клапан
- внутренний блок кондиционера (КВ-N)
- наружный блок (КН-N) на фасаде / в корзине
- трасса фреонопровода и межблочного кабеля
- дренаж конденсата (уклон стрелкой)
- отверстие в наружной стене под трассу

Воздухообмен, м³/ч

№	Помещение	Выт. норма	Выт. проект	Прит. норма	Прит. проект	Устрой-ства
1	Кабинет			32	35	ПК1
2	Санузел	25	25			ВР1
3	Ванная	50	50			ВР2
5	Кухня-столовая	60	60			ВР3
6	Гостиная			60	60	ПК2
7	Спальня			60	60	ПК3
	Итого	**135**	**135**	**152**	**155**	
	Норма по жильцам: 30×2			60		

Воздухообмен квартиры — по большей из сумм притока и вытяжки: норма 152 м³/ч, проект 155 м³/ч.
Приток больше вытяжки на 20 м³/ч — поднять вытяжку.

Кондиционеры

Марка	Помещение	Нар. блок	Трасса, м	Дренаж
КВ-1	6. Гостиная	КН-1	4,7	наружу, i=40 мм/м
КВ-2	7. Спальня	КН-2	0,8	наружу, i=40 мм/м

Привязки — до обмера
Вентканалы в исходных данных не заданы: решётки и вход вытяжки показаны у стояков К1 (вентблок у мокрой зоны). До черновых работ — обмер каналов и проверка тяги; лист перевыпустить по факту.

Примечания


1. Расчёт систем ОВ и подбор оборудования — проектная организация с допуском СРО; лист даёт места, трассы и привязки.
2. Нормы вытяжки — СП 54.13330.2022 (Изм. 1, 2), табл. 7.1: кухня с электроплитой 60 м³/ч, с газовой 100; ванная и совмещённый санузел 50; уборная 25; гардеробная 0,2 ч⁻¹. Приток в жилые — 3 м³/ч на 1 м² (менее 20 м² общей площади на человека), иначе 30 м³/ч на человека.
3. Вентканалы и шахты не сужать, не переносить и не закрывать; вентилятор и кухонная вытяжка через обратный клапан, без перекрытия естественной тяги.
4. Проектные расходы — не ниже нормы, вытяжка сведена с притоком вентиляторами мокрых помещений. Клапаны — в простенке у окна, центр 2000 мм, не над кроватью, не ближе 300 мм к стоякам отопления; типоразмер — на расход.
5. Кухонная вытяжка в воздухообмен не включена: воздуховод не менее Ø125 в коробе, вход в канал отдельный.
6. Переток — зазор под полотнами межкомнатных дверей или переточная решётка.
7. Дренаж кондиционера — непрерывный уклон 40–60 мм/м без контруклонов (СТО НОСТРОЙ 2.23.1-2011, п. 5.8.4); врезка в К1 — через сифон (п. 5.8.9); длина трассы и перепад высот — по паспорту блока; внутренний блок — не ближе 150 мм к потолку, не над кроватью и рабочим местом.
8. Наружный блок на фасаде многоквартирного дома — с согласия собственников (общее имущество); при наличии корзин — только в них. Блоки со * размещены условно.
9. Привязки оборудования — по паспортам приобретённых моделей, до черновых работ.

	Лист	№ док.	Подпись	Дата	
Дизайнер	Кырлан А.С.			04.11.26	

Проект: Квартира 68 м², элитный модерн — **М 1:50**

План вентиляции

Стадия	Лист	Листов
П	41	86

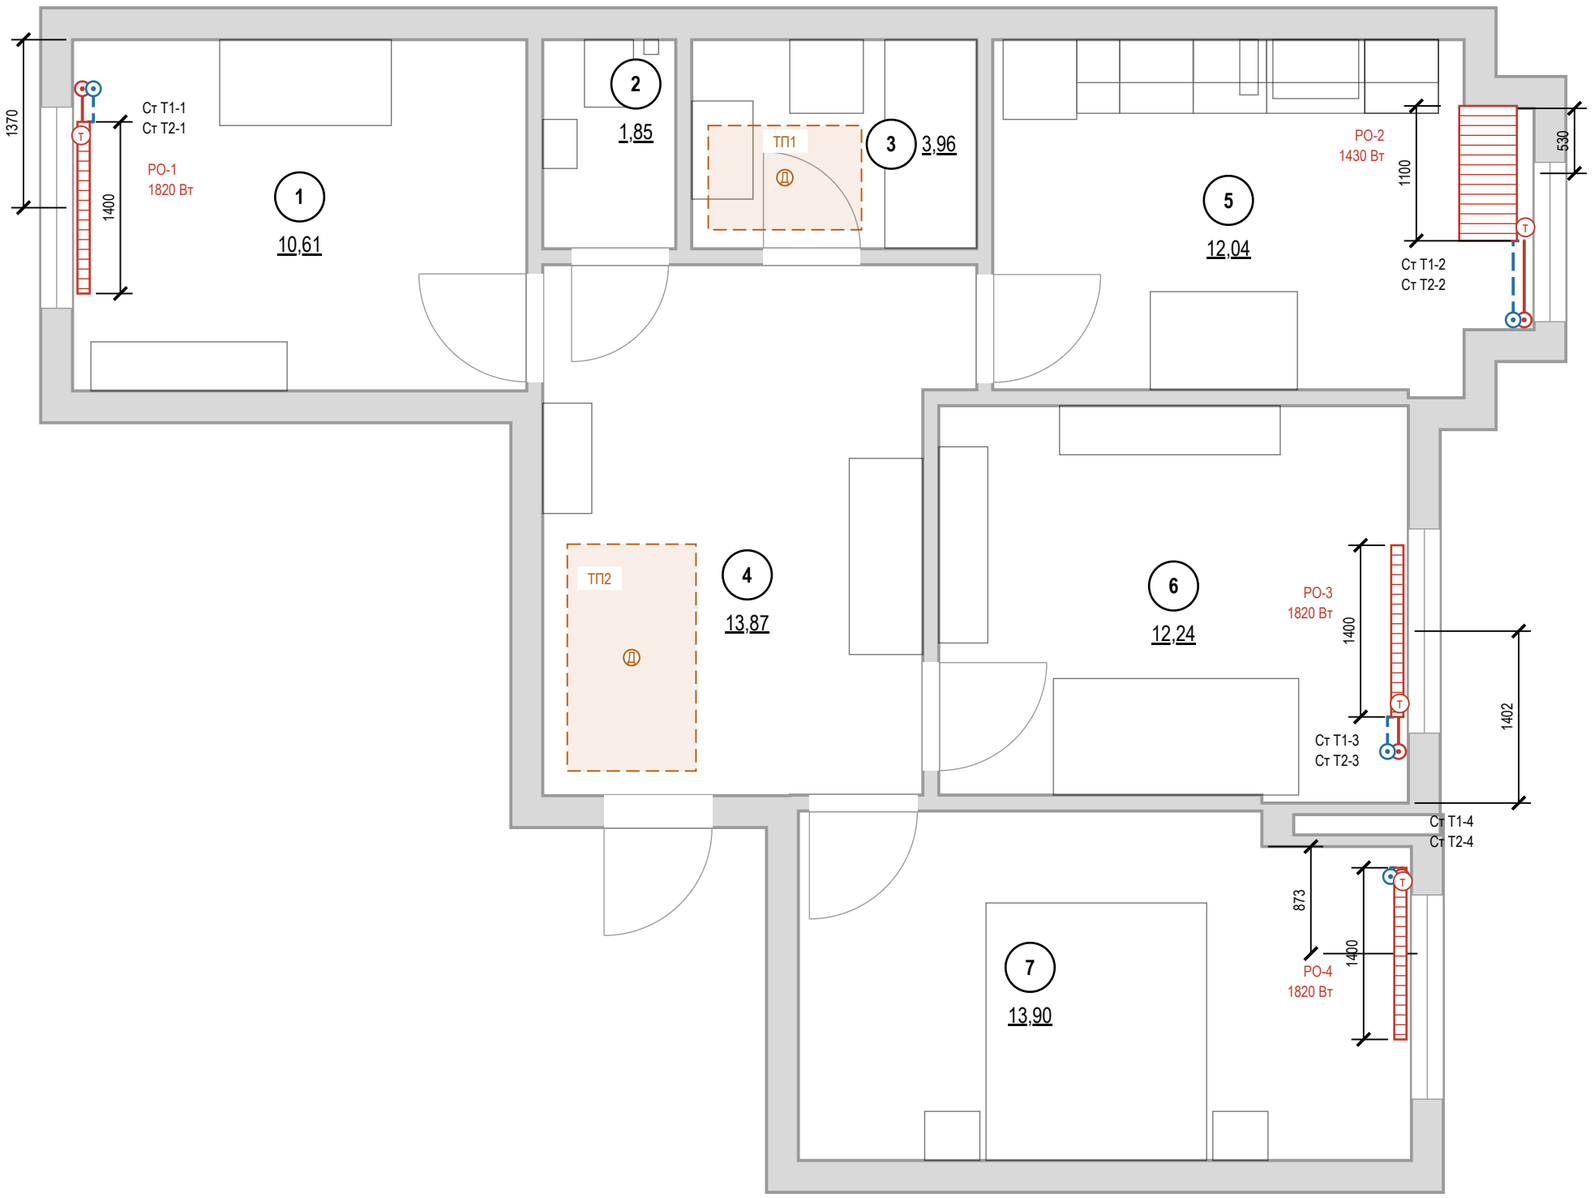

Условные обозначения

- (1) — номер помещения, площадь м²
- радиатор отопления (марка РО-N, длина по плану)
- (Т) — клапан с термоголовкой на подаче
- стояк отопления, подающий (Ст Т1-N)
- стояк отопления, обратный (Ст Т2-N)
- Т1 — отопление, подающий трубопровод
- Т2 — отопление, обратный трубопровод

Ведомость радиаторов

Марка	Помещение	Тип	Д×В×Г, мм	Низ / стена	Q, Вт
РО-1	1. Кабинет	панельный 22	1400×500×100	120 / 40	1820
РО-2	5. Кухня-столовая	панельный 22	1100×500×100	120 / 40	1430
РО-3	6. Гостиная	панельный 22	1400×500×100	120 / 40	1820
РО-4	7. Спальня	панельный 22	1400×500×100	120 / 40	1820

Низ — от чистого пола, стена — зазор до задней панели, мм.

Привязки — до обмера

Стояки отопления в исходных данных не заданы: показаны у откосов окон, подводки — принципиально. До черновых работ — обмер стояков и паспорта приборов; лист перевыпустить по факту.


Примечания

1. Расчёт системы отопления, теплопотерь и подбор приборов — проектная организация с допуском СРО; лист даёт места и привязки.
2. Электрический тёплый пол: ТП1 — пом. 3, мат 1250×850 мм, 160 Вт; ТП2 — пом. 4, мат 1050×1850 мм, 290 Вт; контуры показаны пунктиром; датчик температуры (Д) — в гофротрубе, трасса к терморегулятору — по обмеру. Марка мата и точное положение датчика — при закупке и по обмеру.
3. Тип, длина и мощность радиаторов — по теплотехническому расчёту; лист задаёт места, зазоры и подключение.
4. Зазоры радиатора: низ не менее 100 мм от чистого пола, верх не менее 100 мм до подоконника, 30–50 мм от стены до задней панели; центр по оси окна с допуском ±20 мм. Верх до подоконника — 280 мм.
5. Радиаторы не закрывать глухими коробами и мебелью; перенос и замена приборов в многоквартирном доме — переустройство, согласование с управляющей организацией (ЖК РФ ст. 25–26); вынос на лоджию запрещён.
6. Трубы отопления через межквартирные стены не прокладывать (СП 51.13330.2011, п. 9.19); через перекрытия и перегородки — в гильзах.
7. Привязки приборов и подводок — по паспортам приобретённых радиаторов и клапанов, до черновых работ.
8. До закрытия отделкой трубопроводы отопления испытать гидростатическим давлением с оформлением акта (СП 73.13330.2016, 7.2–7.3).

					Проект: Квартира 68 м², элитный модерн — М 1:50
	Лист	№ док.	Подпись	Дата	
Дизайнер	Кырлан А.С.			04.11.26	План отопления

Стадия	Лист	Листов
П	42	86




Правка к этому листу

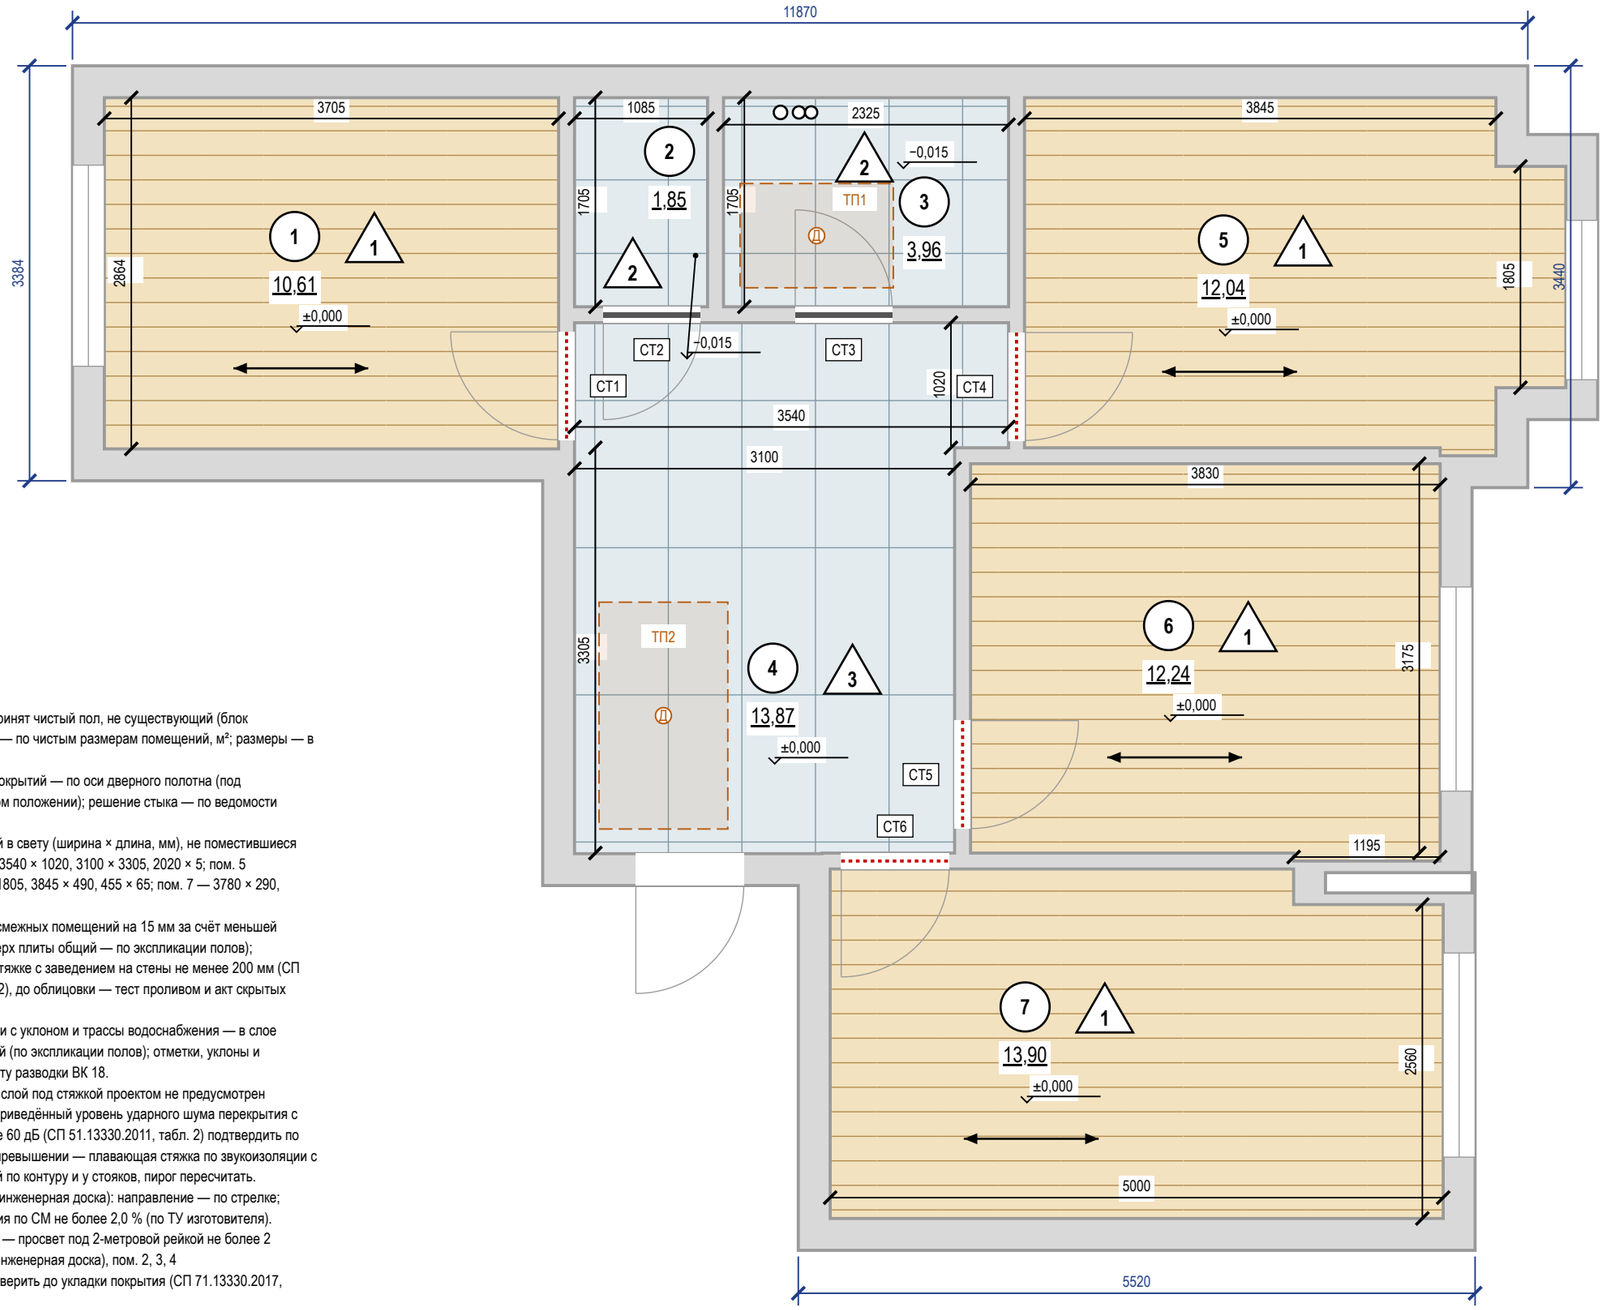

Примечания

1. За отметку ±0,000 принят чистый пол, не существующий (блок отметок). Площади — по чистым размерам помещений, м²; размеры — в мм.
2. Стык разнотипных покрытий — по оси дверного полотна (под полотном в закрытом положении); решение стыка — по ведомости стыков.
3. Размеры помещений в свету (ширина × длина, мм), не поместившиеся на плане: пом. 4 — 3540 × 1020, 3100 × 3305, 2020 × 5; пом. 5 3845 × 560, 4415 × 1805, 3845 × 490, 455 × 65; пом. 7 — 3780 × 290, 5000 × 2560.
4. Пол санузлов ниже смежных помещений на 15 мм за счёт меньшей толщины стяжки (верх плиты общий — по экспликации полов); гидроизоляция по стяжке с заведением на стены не менее 200 мм (СП 29.13330.2011, п. 7.2), до облицовки — тест проливом и акт скрытых работ.
5. Выпуски канализации с уклоном и трассы водоснабжения — в слое засыпки под стяжкой (по экспликации полов); отметки, уклоны и прочистки — по листу разводки ВК 18.
6. Звукоизоляционный слой под стяжкой проектом не предусмотрен (стяжка по плите): приведённый уровень ударного шума перекрытия с полом Lnw не более 60 дБ (СП 51.13330.2011, табл. 2) подтвердить по данным дома; при превышении — плавающая стяжка по звукоизоляции с демпферной лентой по контуру и у стояков, пирог пересчитать.
7. Штучные покрытия (инженерная доска): направление — по стрелке; влажность основания по СМ не более 2,0 % (по ТУ изготовителя).
8. Ровность основания — просвет под 2-метровой рейкой не более 2 мм: пом. 1, 5, 6, 7 (инженерная доска), пом. 2, 3, 4 (керамогранит); проверить до укладки покрытия (СП 71.13330.2017, табл. 8.5).
9. Сетка на плитке — условная, в размер формата; точка старта и раскладка — по листу раскладки плитки.
10. Узор покрытия (заливка-код типа пола) прерывается под надписями — площадями помещений и отметками чистого пола.
11. Электрический тёплый пол: ТП1 — пом. 3, мат 1250×850 мм, 160 Вт; ТП2 — пом. 4, мат 1050×1850 мм, 290 Вт; контуры показаны пунктиром; датчик температуры (Д) — в гофротрубе, трасса к терморегулятору — по обмеру. Марка мата и точное положение датчика — при закупке и по обмеру.
12. Пироги полов — по экспликации полов: слои сверху вниз, толщины в мм; гидроизоляция мокрых зон — в пироге и в ведомости отделки; схема пола — без масштаба.

Экспликация полов

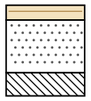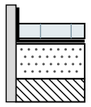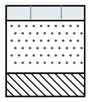Пом.	Тип пола	Схема пола	Элементы пола, толщина, мм	Площадь, м²
1, 5, 6, 7	1		Инженерная доска на клею 14 Стяжка ЦПС М200 — 50 Плита перекрытия Всего 64 мм; ЧП ±0,000, верх плиты −0,064	48,79
2, 3	2		Керамогранит на клею С2 TE S1 — 14 Гидроизоляция обмазочная, 2 слоя, с заведением на стены 200 мм — 2 Стяжка ЦПС М200 — 33 Плита перекрытия Всего 49 мм; ЧП −0,015, верх плиты −0,064	5,81
4	3		Керамогранит на клею С2 TE S1 — 14 Стяжка ЦПС М200 — 50 Плита перекрытия Всего 64 мм; ЧП ±0,000, верх плиты −0,064	13,87
			Итого	**68,47**

Раскладка покрытий

Пом.	Укладка	Старт (оси от чистовых стен), мм	Отступ 1-го ряда / крайние плитки, мм
1	вдоль стен А/В, прямая	от стены А, 1-й ряд вдоль неё	зазор от стены не задан
2	прямая, сетка 600×600, шов 2	ось X 519 от Г; ось Y 829 от А	X 518 / 518; Y 527 / 527
3	прямая, сетка 600×600, шов 2	ось X 1139 от Г; ось Y 829 от А	X 536 / 536; Y 527 / 527
4	прямая, сетка 600×1200, шов 2	ось X 1746 от Г; ось Y 2141 от А	X 541 / 541; Y 938 / 938
5	вдоль стен А/В, прямая	от стены А, 1-й ряд вдоль неё	зазор от стены не задан
6	вдоль стен А/В, прямая	от стены А, 1-й ряд вдоль неё	зазор от стены не задан
7	вдоль стен А/В, прямая	от стены А, 1-й ряд вдоль неё	зазор от стены не задан

Спецификация плинтусов

Наименование	Помещения	Длина, м (с запасом)
Плинтус МДФ под покраску 80×16, крепление к стене, окраска в цвет Farrow & Ball No. 2003	1, 4, 5, 6, 7	71

Отметки по высоте


±0,000	чистый пол пом. 1, 4–7; отсчёт высот
−0,015	чистый пол пом. 2, 3, ниже на 15 мм
−0,064	верх плиты — расчёт, не замер (задание на обмер)
сущ. пол	снимается до плиты; не замерен (задание на обмер)

					Проект: Квартира 68 м², элитный модерн — **М 1:50**
	Лист	№ док.	Подпись	Дата	
Дизайнер	Кырлан А.С.			04.11.26	План покрытий пола


Стадия	Лист	Листов
П	43	86

выпуск 04.11.2026 № f0db2de63c · стр. 43 из 86


Фрагмент 1. Санузел (пом. 2). Пол 600×600, шов 2 мм, М 1:50

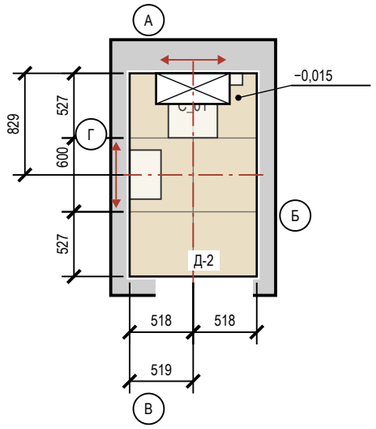

Фрагмент 2. Ванная (пом. 3). Пол 600×600, шов 2 мм, М 1:50

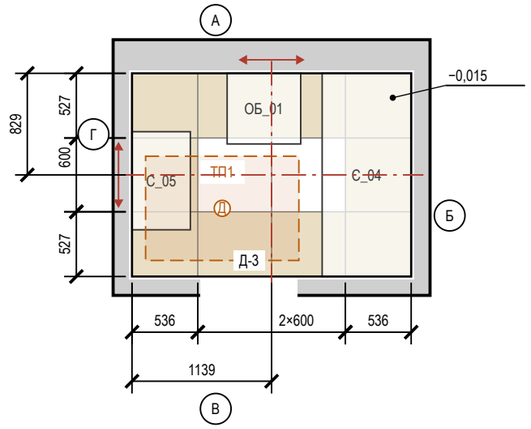

Фрагмент 3. Прихожая (пом. 4). Пол 600×1200, шов 2 мм, М 1:50

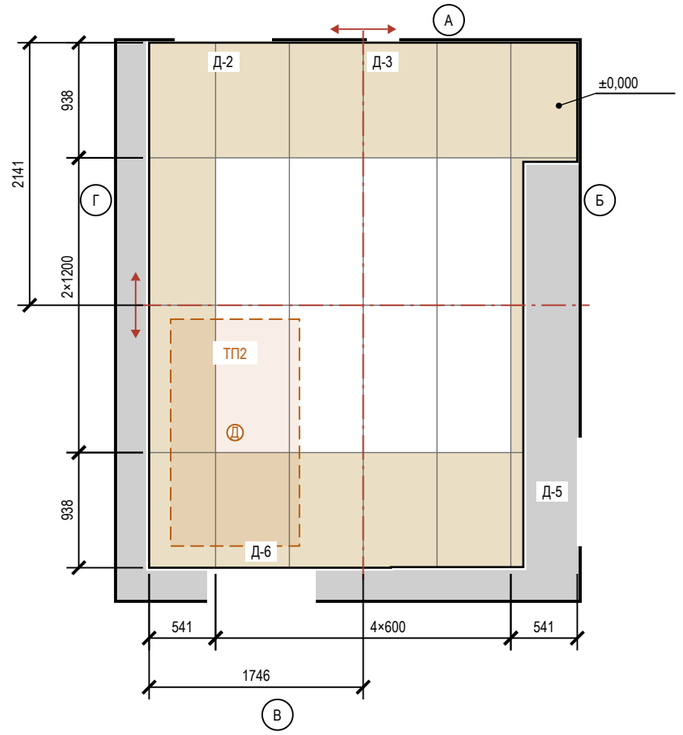

Условные обозначения

- плитка целая; тонкая линия — шов
- плитка с подрезкой (размер — на цепочке)
- ось старта; стрелки — направление укладки
- сантехприбор: габарит, высота по практике
- короб инсталляции: плитка пола — до короба
- электрический тёплый пол: контур мата ТП, Д — датчик
- отметка чистого пола на полке выноски, м
- А — обозначение стены А–Г (как на развёртках)

Примечания

1. Раскладка от чистовых размеров: стены санузлов теряют 10 + 5 + 9 = 24 мм на сторону (штукатурка, клей, плитка); подрезки — чистые, без шва.
2. Старт — от центра помещения (штрихпунктир, стрелки — направление укладки); размер старта — от чистовых стен Г и А.
3. Раскладка фартука «Кухня-столовая» — на листе «Раскладка плитки. Фартук кухни».
4. Калибр партии не задан — до укладки замерить (рабочий размер W, ГОСТ 13996-2019) и пересчитать подрезки.
5. Количество: целые по раскладке + по одной на подрезку, запас 10 %; один артикул — одна партия и тон. Исключены поддон, короб, проёмы и места за коробом; S — по чистым граням: стены нетто = зона облицовки по ведомости отделки − место за коробом инсталляции 0,72 м² (плитку за коробом не кладут), короб — отдельной строкой.
6. Клей C2 TE S1 Ceresit CM 17; C2 TE S1 (ГОСТ Р 56387-2018), затирка CG2WA Mapei Ultracolor Plus 132; CG2WA; расход — по ТУ выбранной марки.
7. Гидроизоляция: пол и стены 200 мм от ЧП; над ванной — до 2000 и 300 мм за борт (пом. 3) (см. развёртки); акт скрытых работ, пролив 24 ч.
8. Электрический тёплый пол: ТП1 — пом. 3, мат 1250×850 мм, 160 Вт; ТП2 — пом. 4, мат 1050×1850 мм, 290 Вт; контуры показаны пунктиром; датчик температуры (Д) — в гофротрубе, трасса к терморегулятору — по обмеру. Марка мата и точное положение датчика — при закупке и по обмеру. Плитку над матом клеить клеем, который изготовитель допускает для тёплого пола, до включения выдержать срок по ТУ клея.
9. Швы пола совмещены со швами стены А; по периметру — демпферная лента.
10. Отметка чистого пола −0,015, порог 15 мм; стык с соседним покрытием — по оси полотна двери.

Ведомость плитки

Помещение, поверхность	Плитка, код	Формат	Шов	S, м²	Целых	Подр.	С запасом
Санузел, пол	аналог: керамогранит под травертин	600×600	2	1,85	0	6	7
Санузел, стены А–Г	аналог: керамогранит под травертин	600×1200	2	11,04	4	16	24
Санузел, короб инсталляции	аналог: керамогранит под травертин	600×1200	2	1,47	1	3	5
Ванная, пол	аналог: керамогранит под травертин	600×600	2	3,96	2	10	14
Ванная, стены А–Г	аналог: керамогранит под травертин	600×1200	2	17,72	8	20	32
Прихожая, пол	аналог: керамогранит ректифицированный под травертин, матовый	600×1200	2	13,87	8	16	27
Кухня-столовая, фартук (ст. А)	аналог: керамогранит под травертин, матовый	1200×600	2	1,68	0	5	6
Итого 600×600				5,81	2	16	21
Итого 600×1200				**45,78**	**21**	**60**	**94**


Ведомость материалов

Материал	Класс, код	Норма расхода	Кол-во
Затирка	CG2WA Mapei Ultracolor Plus 132	(a+b)/ab·шов·t·1,6	4,0 кг
Затирка	CG2WA	(a+b)/ab·шов·t·1,6	0,1 кг
Клей	C2 TE S1 Ceresit CM 17	1,5 кг/м²·мм, слой 5	398 кг (16 меш.)
Клей	C2 TE S1	1,5 кг/м²·мм, слой 5	14 кг (1 меш.)
Гидроизоляция	обмазочная, 2 слоя: пол, стены по периметру и зоны замачивания	по ТУ	15,8 м²
Демпф. лента	по периметру пола из плитки		26,9 м

					Проект: Квартира 68 м², элитный модерн	**М 1:50**
	Лист	№ док.	Подпись	Дата		
Дизайнер	Кырлан А.С.			04.11.26	Раскладка плитки. Планы полов	Стадия: П; Лист: 44; Листов: 86

выпуск 04.11.2026 № f0db2de63c · стр. 44 из 86

Фрагмент 1. Кухня-столовая (пом. 5), фартук, стена А. 1200×600, шов 2 мм, М 1:20

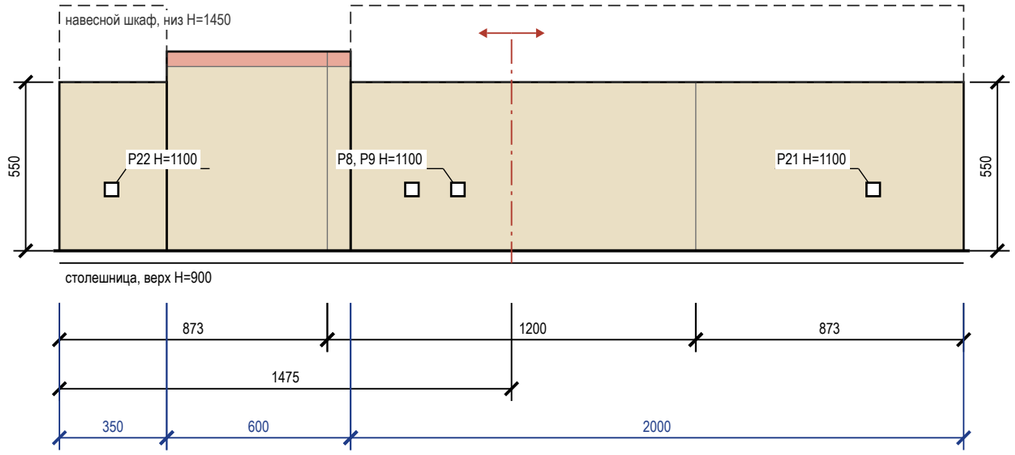

Условные обозначения

- плитка целая; тонкая линия — шов
- плитка с подрезкой (размер — на цепочке)
- ось старта; стрелки — направление укладки
- электроточка: марка и H — по листам ЭОМ
- столешница (верх)
- навесной шкаф над фартуком

Подсчёт плитки

Поверхность	Формат	S, м²	Целых	Подр.	С запасом
Кухня-столовая, фартук (ст. А)	1200×600	1,68	0	5	6

Сдвиг розеток фартука под раскладку

Точка (ЭОМ)	Сейчас: от края фартука / H	Под раскладку: от края / H	Сдвиг, мм
P8, P9, P22	1150, 1300, 170 / 1100	1150, 1300, 170 / 1175	H +75 — ось ряда
P21	2655 / 1100	2655 / 1175	H +75 — ось ряда

Примечания

1. Фартук, Кухня-столовая: 1200×600 горизонтально, шов 2 мм; зоны 350 мм — 900…1450, 600 мм — 900…1550, 2000 мм — 900…1450 (от столешницы до низа навесного шкафа, без шкафа — 650 мм). Старт от центра участка, подрезки 873 мм. Площадь 1,68 м² — как в ведомости отделки.
2. Фартук — после монтажа столешницы, низ на 2–3 мм выше неё, шов со столешницей — санитарный герметик; навесные шкафы — после фартука. Торцы у пенала и стены — профиль или запил 45°.
3. Фартук, Кухня-столовая: в зоне до отм. 1550 верхний ряд подрезан 48 мм — меньше 1/3 плитки; полоса прикрыта корпусом навесного модуля и на виду не остаётся. Раскладкой не снимается: убрать подрезку можно, только выровняв низ этого модуля с соседними (1450 мм) — решение мебельщика.
4. Розетки из таблицы переносятся до черновой электрики: по высоте — на ось ряда плитки, от вертикального шва крупной плитки — не ближе 60 мм. Привязка — от левого края фартука на развёртке.
5. Клей, затирка и итог по форматам — в ведомостях листа «Раскладка плитки. Планы полов».

					Проект: Квартира 68 м², элитный модерн	**М 1:20**
	Лист	№ док.	Подпись	Дата		
Дизайнер	Кырлан А.С.			04.11.26	Раскладка плитки. Фартук кухни	Стадия: П; Лист: 45; Листов: 86

Правка к этому листу

Развёртка стены А


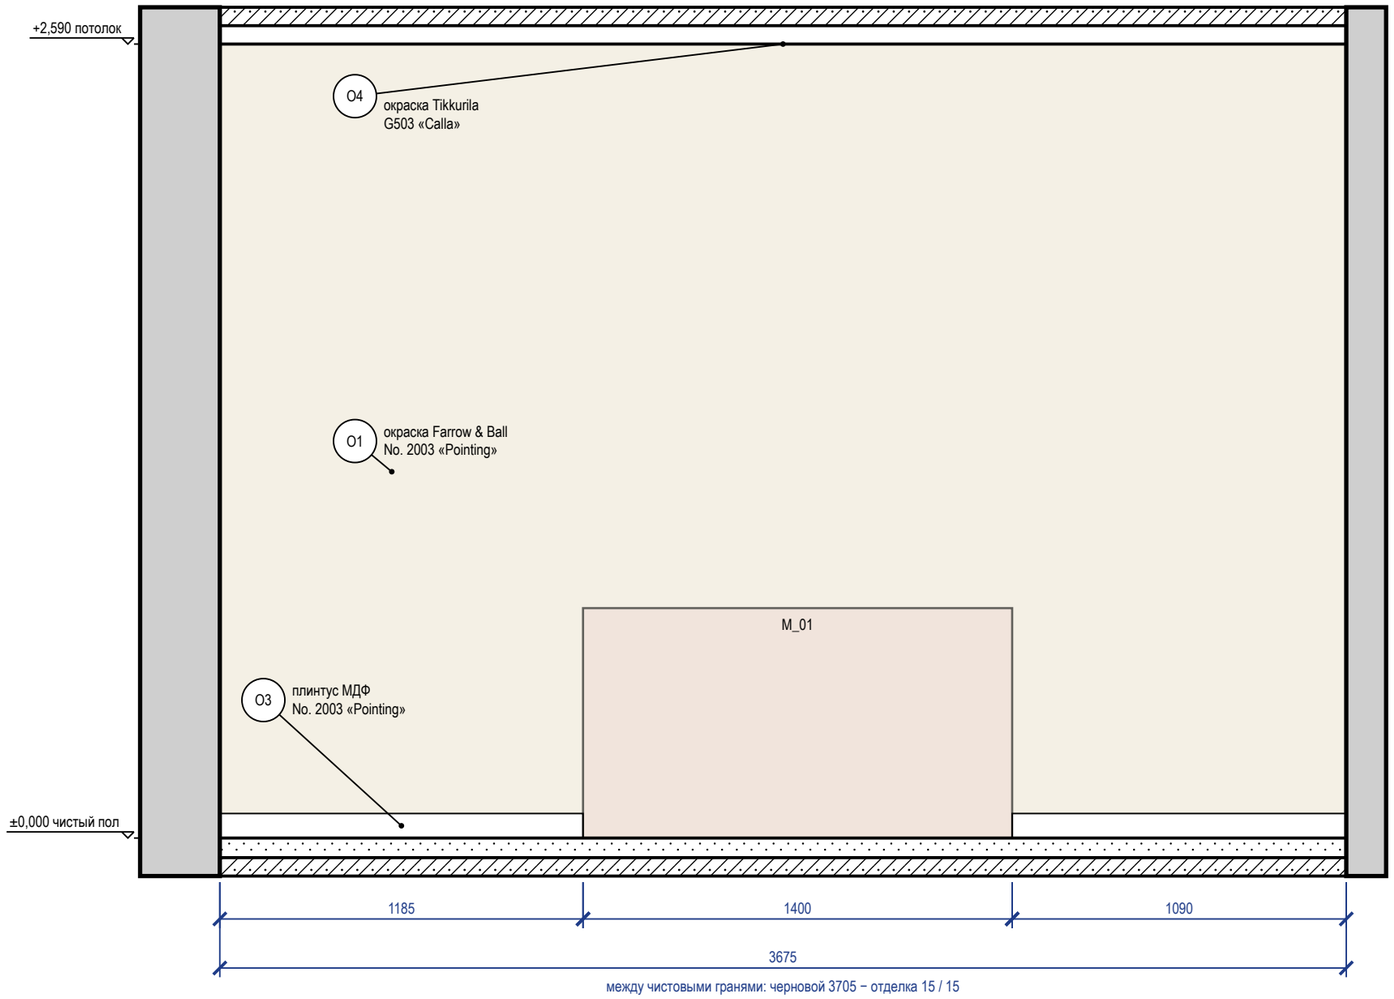


Схема развёрток (М 1:100)

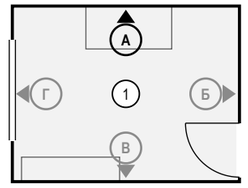

Ведомость отделки (на листе)

Марка	Поверхность	Материал, изделие	Цвет, код	Кол.
О1	стены	окраска, Farrow & Ball Modern Emulsion, матовая, подготовка Q3	Farrow & Ball No. 2003 «Pointing»	9,5 м²
О3	плинтус	плинтус МДФ, h 80 мм, аналог: плинтус МДФ под покраску 80×16	Farrow & Ball No. 2003 «Pointing»	2,3 м
О4	потолок	окраска, Tikkurila Euro Power 7, глубокоматовая, подготовка Q3	Tikkurila G503 «Calla»	10,6 м²

Примечания

1. Размеры — в мм от чистовых поверхностей стен; условные обозначения и общие указания — лист 4.
2. Стена А показана двумя видами: здесь — архитектурная развёртка (мебель, отделка, проёмы, высоты), электроточки и выводы ВК с привязками и таблицей — на листе 47 («Привязки»).

	Лист	№ док.	Подпись	Дата
Дизайнер	Кырлан А.С.			04.11.26

Проект: Квартира 68 м², элитный модерн — **М 1:20**

Развёртка стены А. Кабинет (пом. 1)

Стадия	Лист	Листов
П	46	86

Правка к этому листу

Развёртка стены А: электроточки и выводы

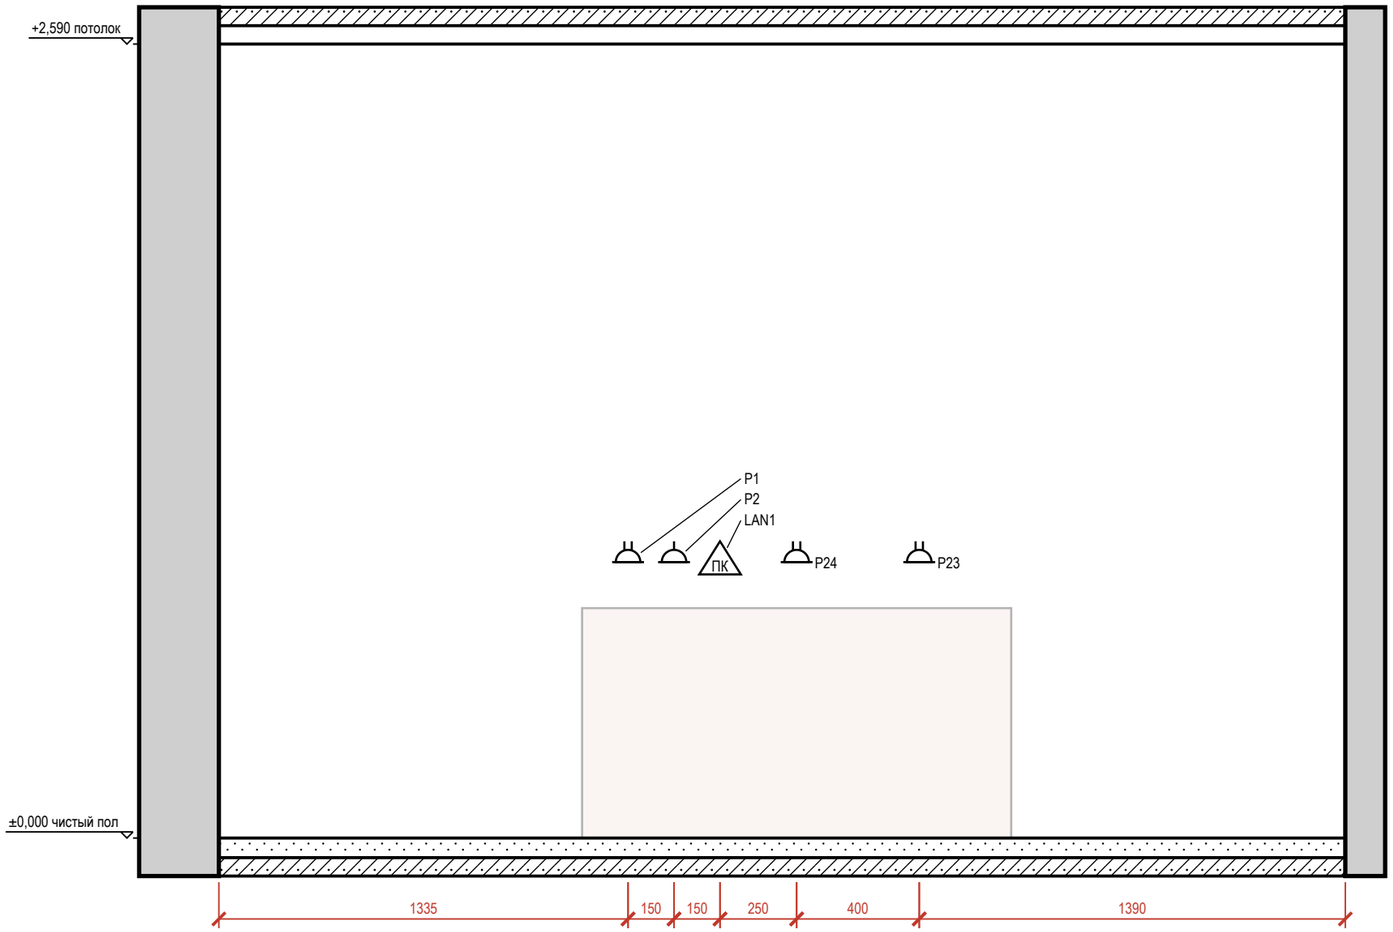



Таблица привязок электроточек и выводов

Марка	Назначение	От угла, мм	Н от пола, мм	Примечание
P1	розетка: рабочий стол	1335	900	рамка 2 поста, гр. 3
P2	розетка: рабочий стол: монитор	1485	900	гр. 3
LAN1	розетка RJ45: рабочий стол	1635	900	
P24	розетка: рабочий стол: компьютер, монитор, зарядки	1885	900	рамка 2 поста, гр. 3
P23	розетка: рабочий стол: компьютер, монитор, зарядки	2285	900	рамка 2 поста, гр. 3

Условные обозначения

- розетка с заземляющим контактом; у знака — марка, ×N постов в рамке, гр. — группа щита, Н — высота оси, мм
- ПК — розетка компьютерная RJ45
- привязки точек и выводов от угла и от пола, мм
- А — марка развёртки: буква стены, стрелка — взгляд

Схема развёрток (М 1:50)

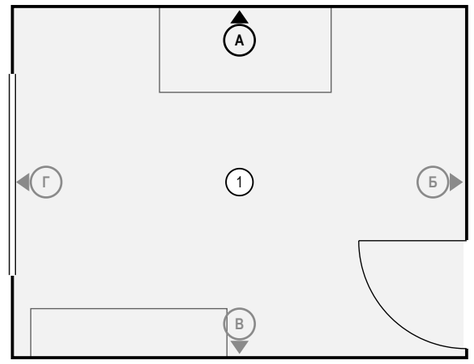

Примечания

1. Вид «Привязки» стены А — электроточки и выводы ВК; архитектурная развёртка (мебель, отделка, проёмы, высоты) — на листе 46. Мебель и приборы — подложкой для ориентира; их марки и обозначения мебели, проёмов и стен — там же.
2. Привязки — в мм: по горизонтали от левого чистового угла стены до оси изделия, Н — от чистого пола до оси; все точки — в таблице привязок. Красная цепочка — привязки по осям; точки ближе 120 мм одна к другой в цепочку не дробятся — их привязки только в таблице.
3. У знака — марка электроточки (Р — розетка, S — выключатель, Св — светильник, ЭВ — вывод кабеля); условные обозначения и общие указания — лист 4.

	Лист	№ док.	Подпись	Дата
Дизайнер	Кырлан А.С.			04.11.26

Проект: Квартира 68 м², элитный модерн — **М 1:20**

Привязки электроточек, стена А. Кабинет (пом. 1)

Стадия	Лист	Листов
П	47	86

выпуск 04.11.2026 № f0db2de63c · стр. 47 из 86

Правка к этому листу

Развёртка стены Б


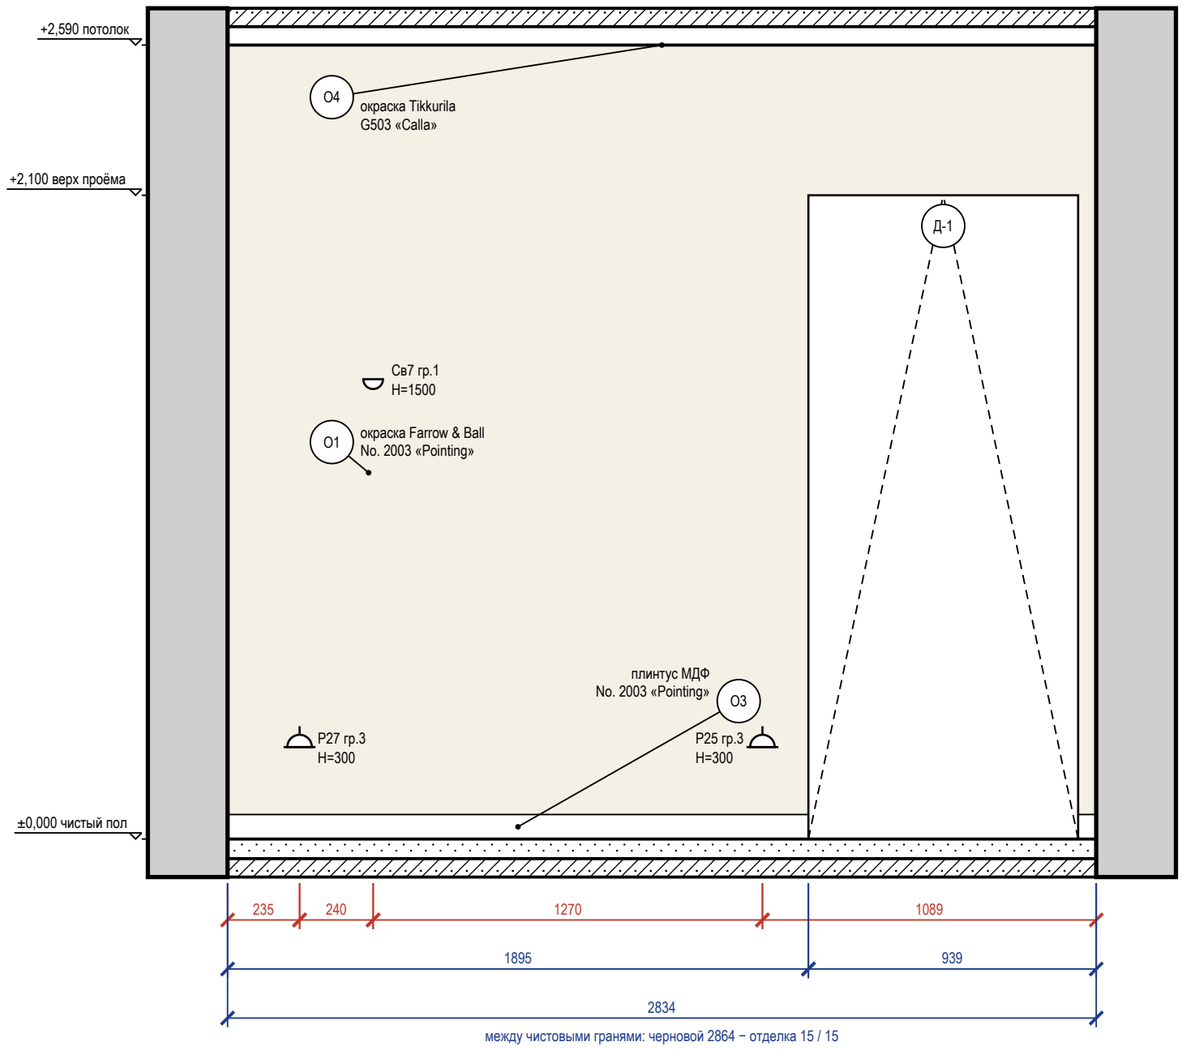


Схема развёрток (М 1:100)

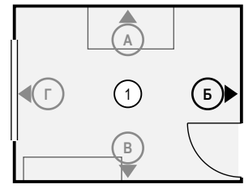

Ведомость отделки (на листе)

Марка	Поверхность	Материал, изделие	Цвет, код	Кол.
О1	стены	окраска, Farrow & Ball Modern Emulsion, матовая, подготовка Q3	Farrow & Ball No. 2003 «Pointing»	5,5 м²
О3	плинтус	плинтус МДФ, h 80 мм, аналог: плинтус МДФ под покраску 80×16	Farrow & Ball No. 2003 «Pointing»	2 м
О4	потолок	окраска, Tikkurila Euro Power 7, глубокоматовая, подготовка Q3	Tikkurila G503 «Calla»	10,6 м²

Примечания

1. Размеры — в мм от чистовых поверхностей стен; условные обозначения и общие указания — лист 4.

					Проект: Квартира 68 м², элитный модерн	М 1:20
	Лист	№ док.	Подпись	Дата		
Дизайнер	Кырлан А.С.			04.11.26	Развёртка стены Б. Кабинет (пом. 1)	Стадия: П; Лист: 48; Листов: 86

выпуск 04.11.2026 № f0db2de63c · стр. 48 из 86

Правка к этому листу

Развёртка стены В


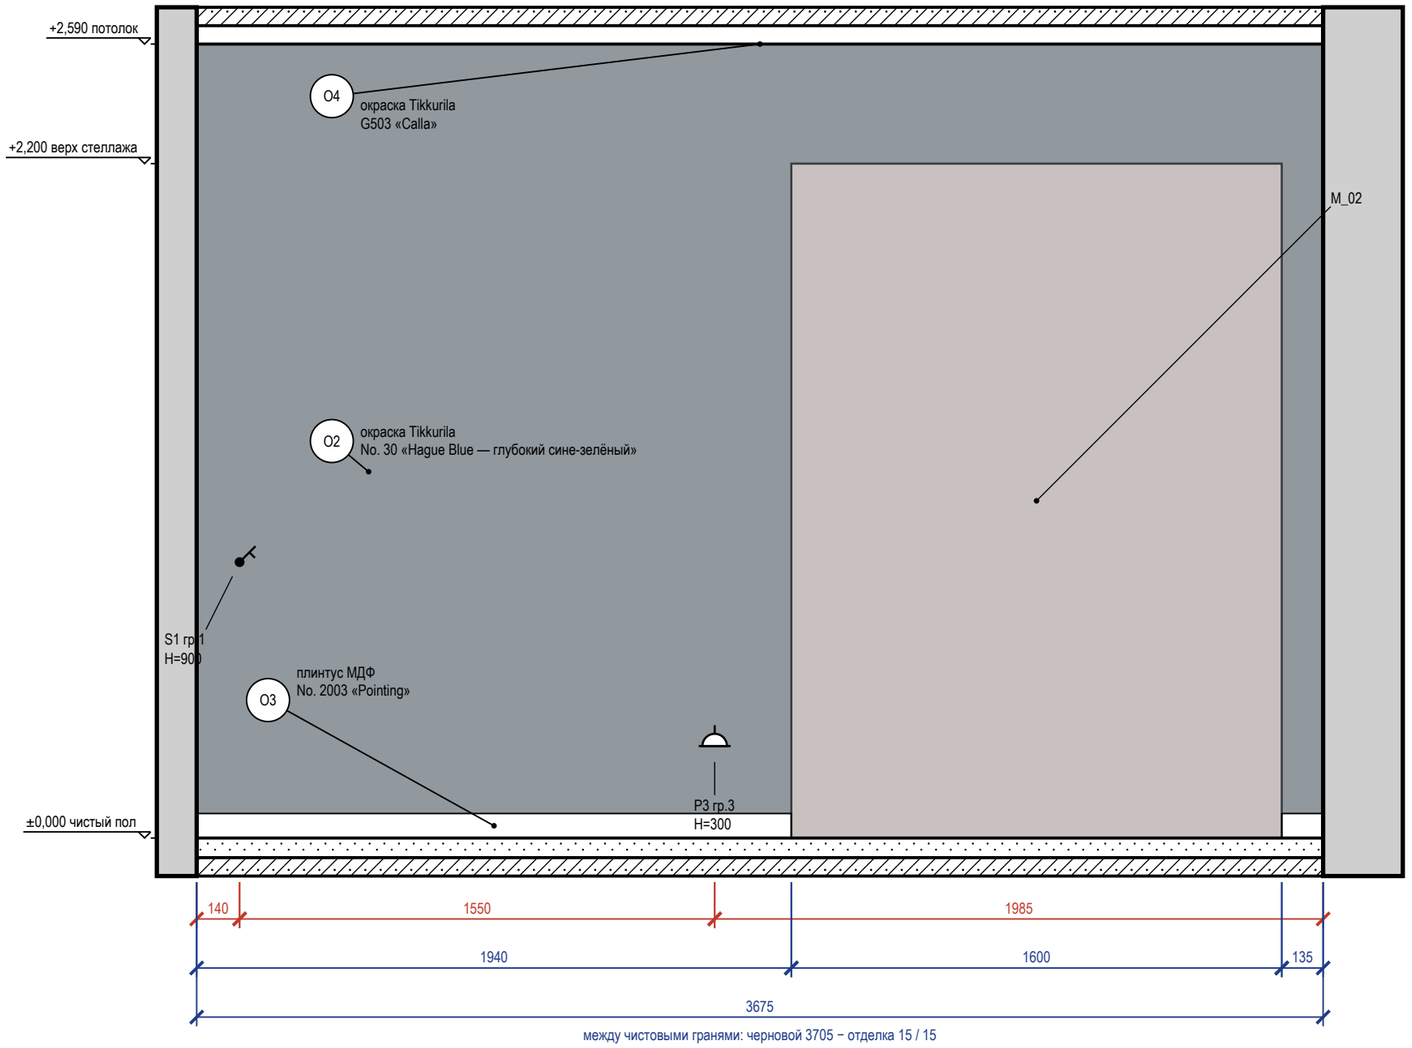


Схема развёрток (М 1:100)

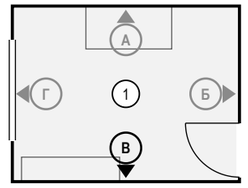

Ведомость отделки (на листе)

Марка	Поверхность	Материал, изделие	Цвет, код	Кол.
O2	акцентная стена	окраска, Tikkurila Euro Power 7, колеровка по NCS, матовая, подготовка Q3	Farrow & Ball No. 30 «Hague Blue глубокий сине-зелёный»	9,5 м²
O3	плинтус	плинтус МДФ, h 80 мм, аналог: плинтус МДФ под покраску 80×16	Farrow & Ball No. 2003 «Pointing»	2,1 м
O4	потолок	окраска, Tikkurila Euro Power 7, глубокоматовая, подготовка Q3	Tikkurila G503 «Calla»	10,6 м²

Примечания

1. Размеры — в мм от чистовых поверхностей стен; условные обозначения и общие указания — лист 4.

					Проект: Квартира 68 м², элитный модерн	М 1:20
	Лист	№ док.	Подпись	Дата		
Дизайнер	Кырлан А.С.			04.11.26	Развёртка стены В. Кабинет (пом. 1)	Стадия: П; Лист: 49; Листов: 86

Правка к этому листу

Развёртка стены Г


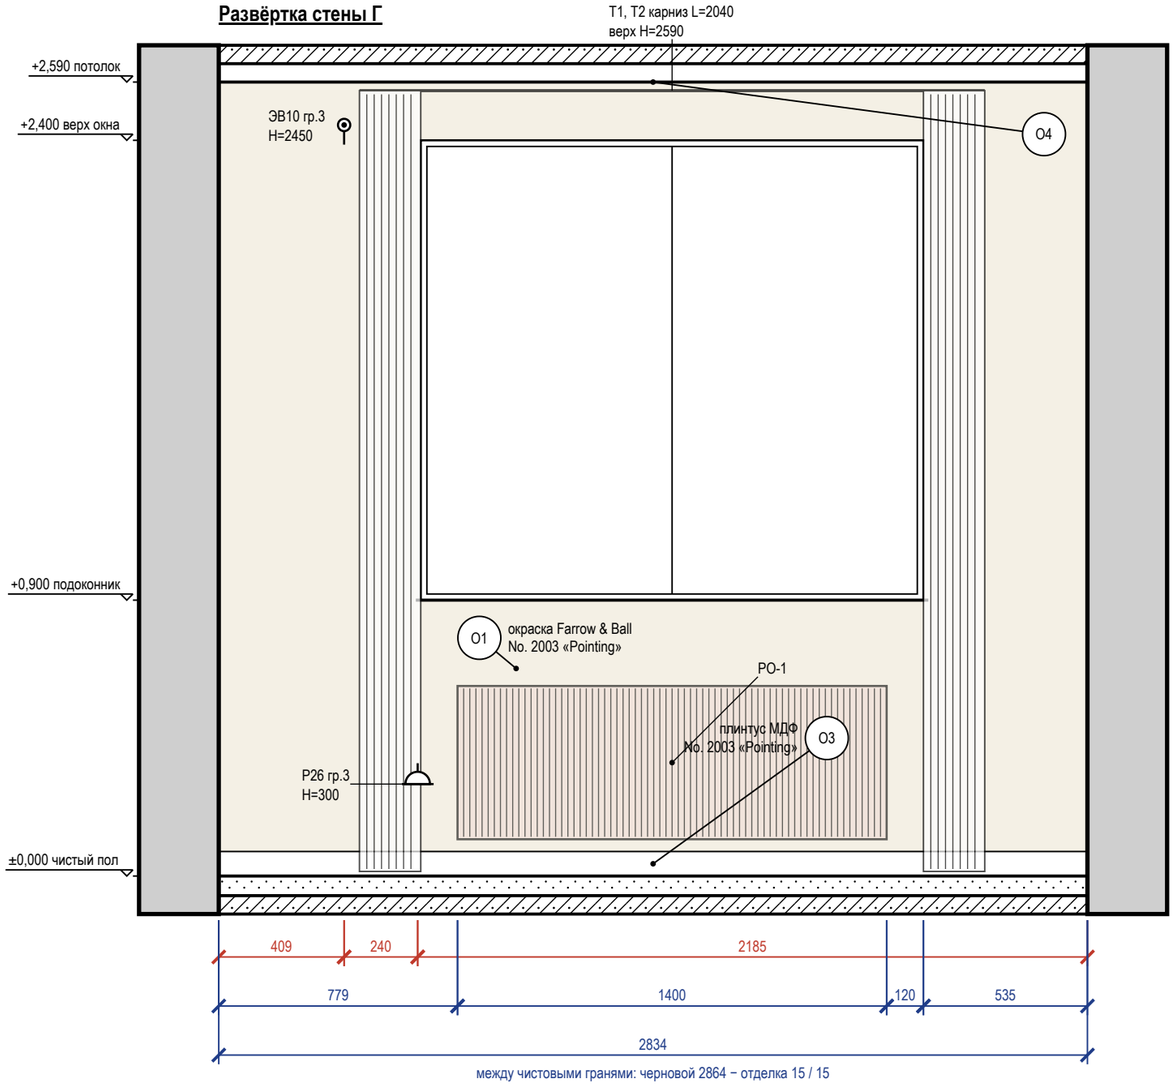


Схема развёрток (М 1:100)

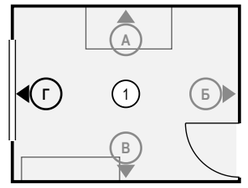

Ведомость отделки (на листе)


Марка	Поверхность	Материал, изделие	Цвет, код	Кол.
O1	стены	окраска, Farrow & Ball Modern Emulsion, матовая, подготовка Q3	Farrow & Ball No. 2003 «Pointing»	4,9 м²
O3	плинтус	плинтус МДФ, h 80 мм, аналог: плинтус МДФ под покраску 80×16	Farrow & Ball No. 2003 «Pointing»	2,8 м
O4	потолок	окраска, Tikkurila Euro Power 7, глубокоматовая, подготовка Q3	Tikkurila G503 «Calla»	10,6 м²

Примечания

1. Размеры — в мм от чистовых поверхностей стен; условные обозначения и общие указания — лист 4.
2. Карнизы (шины) — по ведомости текстиля декоратора: длина L и верх H на развёртке — те же числа, что в ведомости; крепление — до окраски потолка.


					Проект: Квартира 68 м², элитный модерн	М 1:20
	Лист	№ док.	Подпись	Дата		
Дизайнер	Кырлан А.С.			04.11.26	Развёртка стены Г. Кабинет (пом. 1)	Стадия: П; Лист: 50; Листов: 86

Развёртка стены А

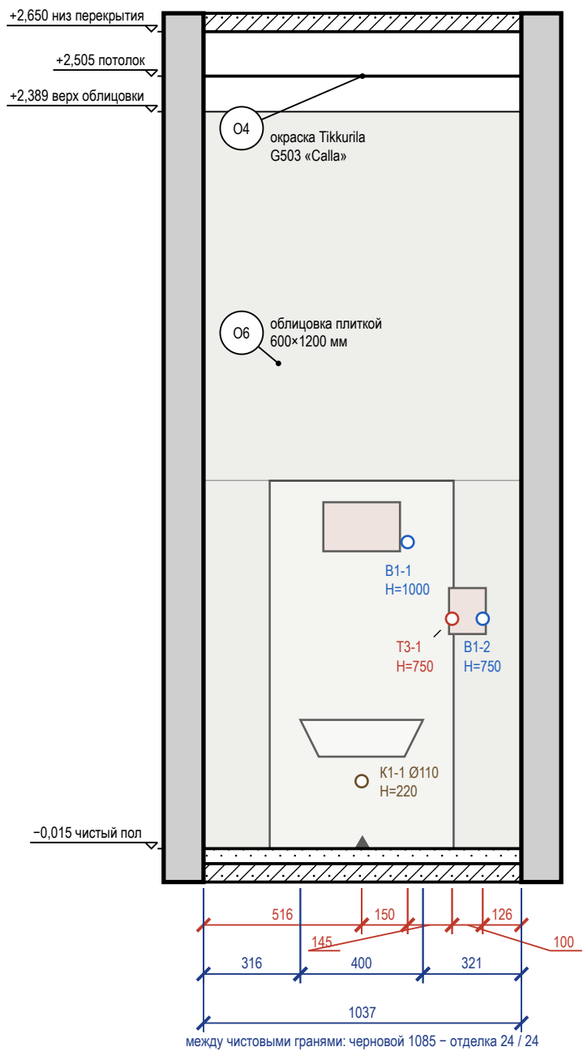


между чистовыми гранями: черновой 1085 − отделка 24 / 24

Развёртка стены Б

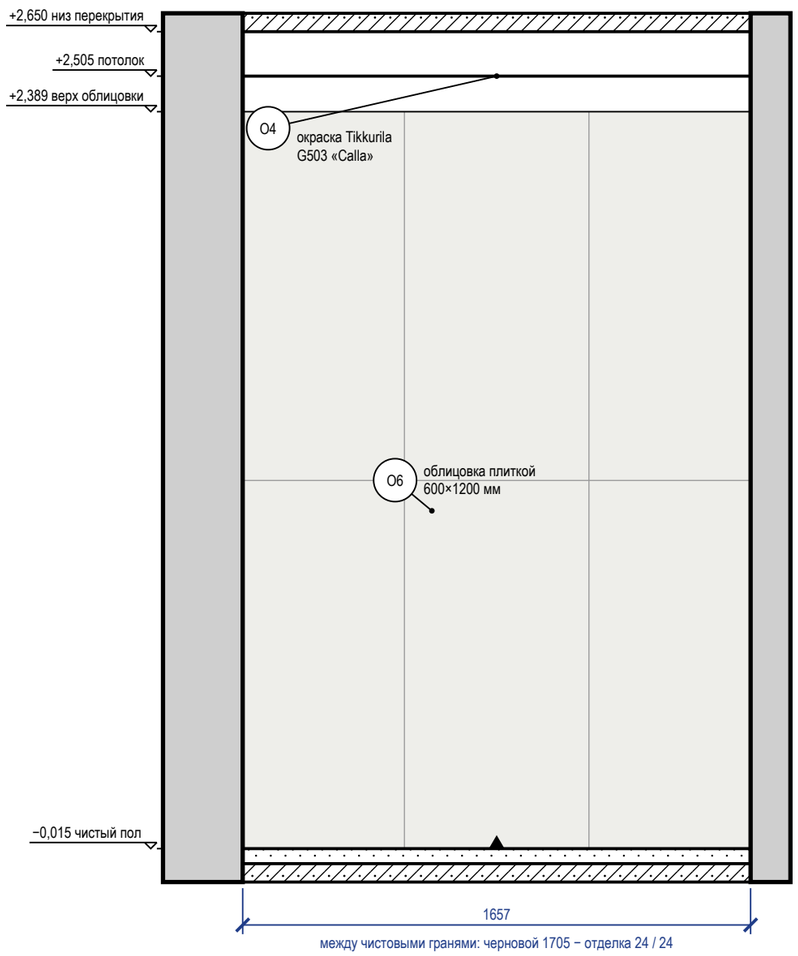


между чистовыми гранями: черновой 1705 − отделка 24 / 24

Развёртка стены В

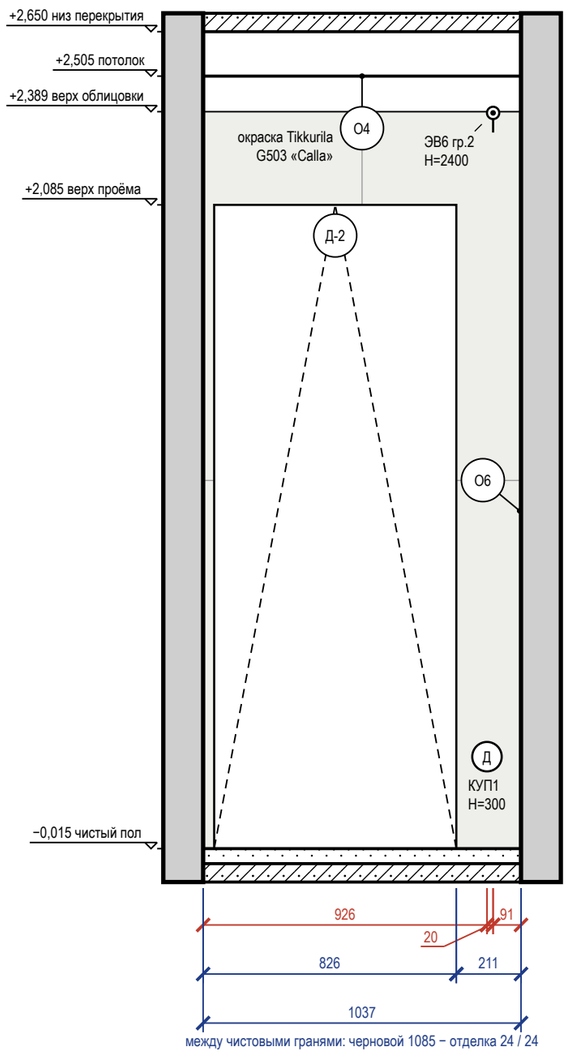

между чистовыми гранями: черновой 1085 − отделка 24 / 24

Схема развёрток (М 1:100)

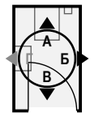

Ведомость отделки (на листе)

Марка	Поверхность	Материал, изделие	Цвет, код	Кол.
О4	потолок	окраска, Tikkurila Euro Power 7, матовая, подготовка Q3	Tikkurila G503 «Calla»	1,9 м²
О6	стены	облицовка плиткой, 600×1200×9 мм, аналог: керамогранит под травертин, матовый, затирка CG2WA		7,3 м²

Визуализация этой стены — лист 3



Примечания

1. Размеры — в мм от чистовых поверхностей стен; условные обозначения и общие указания — лист 4.
2. Схема мебели, приборов и декора не является технической документацией для производства мебели; габариты — по паспортам изделий.
3. Облицовка — по сетке швов 2 мм, раскладка от оси стены (треугольник у пола), целые ряды от пола; подрезки — по листу раскладки плитки.
4. Гидроизоляция в 2 слоя, заход на стены 200 мм — до облицовки, с актом скрытых работ и тестом проливом (узел — на листе узлов).

	Лист	№ док.	Подпись	Дата
Дизайнер	Кырлан А.С.			04.11.26

Проект: Квартира 68 м², элитный модерн — М 1:20

Развёртки стен А, Б, В. Санузел (пом. 2)

Стадия	Лист	Листов
П	51	86

Правка к этому листу

Развёртка стены Г


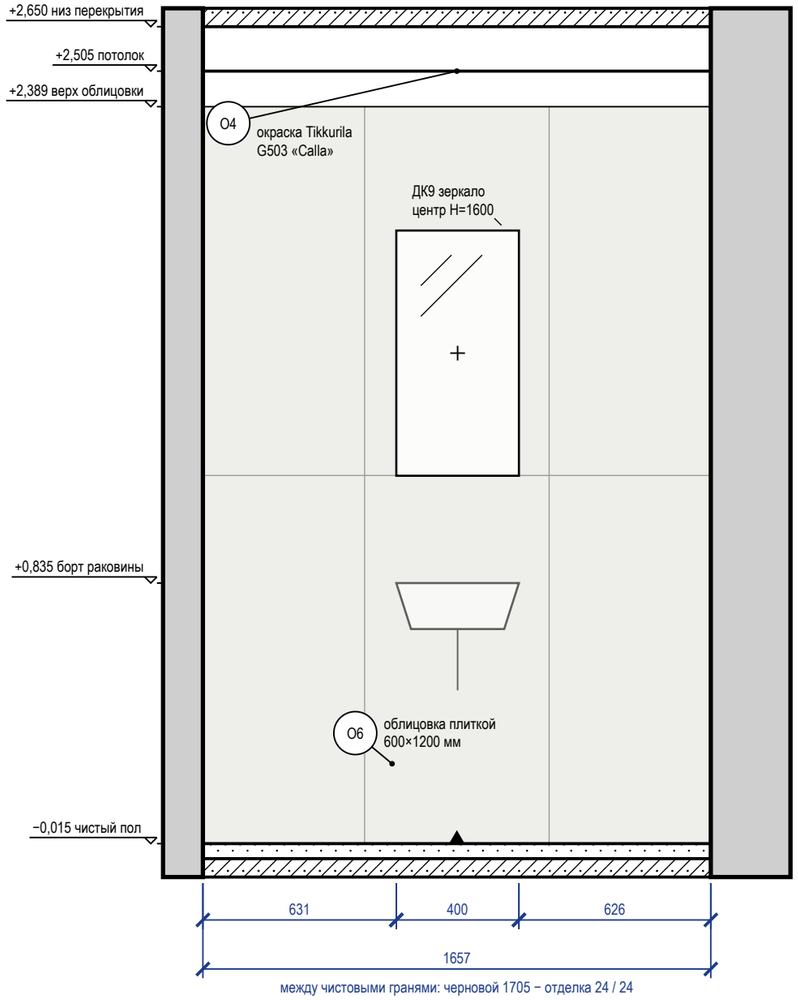


Схема развёрток (М 1:100)

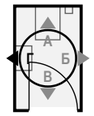

Ведомость отделки (на листе)

Марка	Поверхность	Материал, изделие	Цвет, код	Кол.
О4	потолок	окраска, Tikkurila Euro Power 7, матовая, подготовка Q3	Tikkurila G503 «Calla»	1,9 м²
О6	стены	облицовка плиткой, 600×1200×9 мм, аналог: керамогранит под травертин, матовый, затирка CG2WA		4 м²

Примечания

1. Размеры — в мм от чистовых поверхностей стен; условные обозначения и общие указания — лист 4.
2. Стена Г показана двумя видами: здесь — архитектурная развёртка (мебель, отделка, проёмы, высоты), электроточки и выводы ВК с привязками и таблицей — на листе 53 («Привязки»).
3. Облицовка — по сетке швов 2 мм, раскладка от оси стены (треугольник у пола), целые ряды от пола; подрезки — по листу раскладки плитки.
4. Гидроизоляция в 2 слоя, заход на стены 200 мм — до облицовки, с актом скрытых работ и тестом проливом (узел — на листе узлов).
5. Картины и зеркала крепить к основанию по паспорту изделия (закладные и анкеры — в перечне скрытых работ); крест — ось центра предмета.

					Проект: Квартира 68 м², элитный модерн	М 1:20
	Лист	№ док.	Подпись	Дата		
Дизайнер	Кырлан А.С.			04.11.26	Развёртка стены Г. Санузел (пом. 2)	Стадия: П; Лист: 52; Листов: 86

Правка к этому листу

Развёртка стены Г: электроточки и выводы

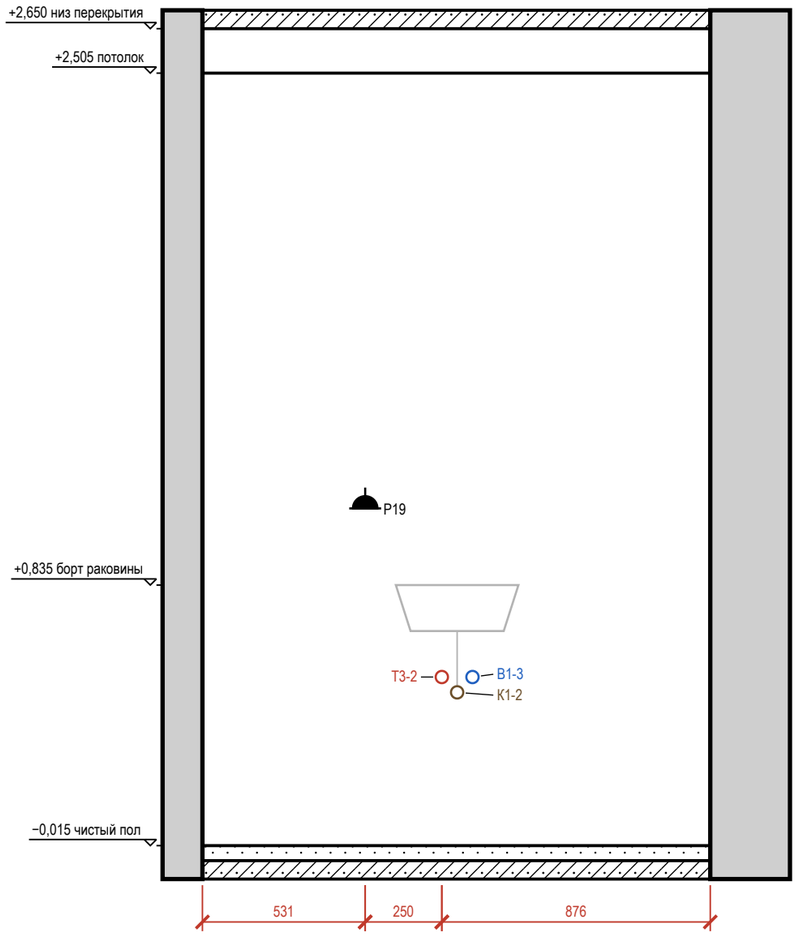



Таблица привязок электроточек и выводов

Марка	Назначение	От угла, мм	H от пола, мм	Примечание
P19	розетка: розетка у раковины (фен, зона 3)	531	1100	гр. 15, IP44
T3-2	горячая вода — умывальник	781	550	межос. 100
K1-2	канализация — умывальник	831	500	Ø40
B1-3	холодная вода — умывальник	881	550	межос. 100

Условные обозначения

- розетка влагозащищённая IP44
- вывод B1 (код — в ведомости привязок)
- вывод T3 (код — в ведомости привязок)
- вывод K1 (код — в ведомости привязок)
- привязки точек и выводов от угла и от пола, мм
- марка развёртки: буква стены, стрелка — взгляд

Схема развёрток (М 1:50)

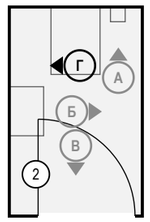


Примечания

1. Вид «Привязки» стены Г — электроточки и выводы ВК; архитектурная развёртка (мебель, отделка, проёмы, высоты) — на листе 52. Мебель и приборы — подложкой для ориентира; их марки и обозначения мебели, проёмов и стен — там же.
2. Привязки — в мм: по горизонтали от левого чистового угла стены до оси изделия, H — от чистого пола до оси; все точки — в таблице привязок. Красная цепочка — привязки по осям; точки ближе 120 мм одна к другой в цепочку не дробятся — их привязки только в таблице.
3. У знака — марка электроточки (P — розетка, S — выключатель, Св — светильник, ЭВ — вывод кабеля); условные обозначения и общие указания — лист 4.
4. Коды выводов ВК: B1 — холодная вода, T3 — горячая вода, K1 — канализация; номер после дефиса — номер вывода на листе выводов сантехники.

					Проект: Квартира 68 м², элитный модерн	М 1:20
	Лист	№ док.	Подпись	Дата		
Дизайнер	Кырлан А.С.			04.11.26	Привязки электроточек и выводов ВК, стена Г. Санузел (пом. 2)	Стадия: П; Лист: 53; Листов: 86


выпуск 04.11.2026 № f0db2de63c · стр. 53 из 86

Развёртка стены А

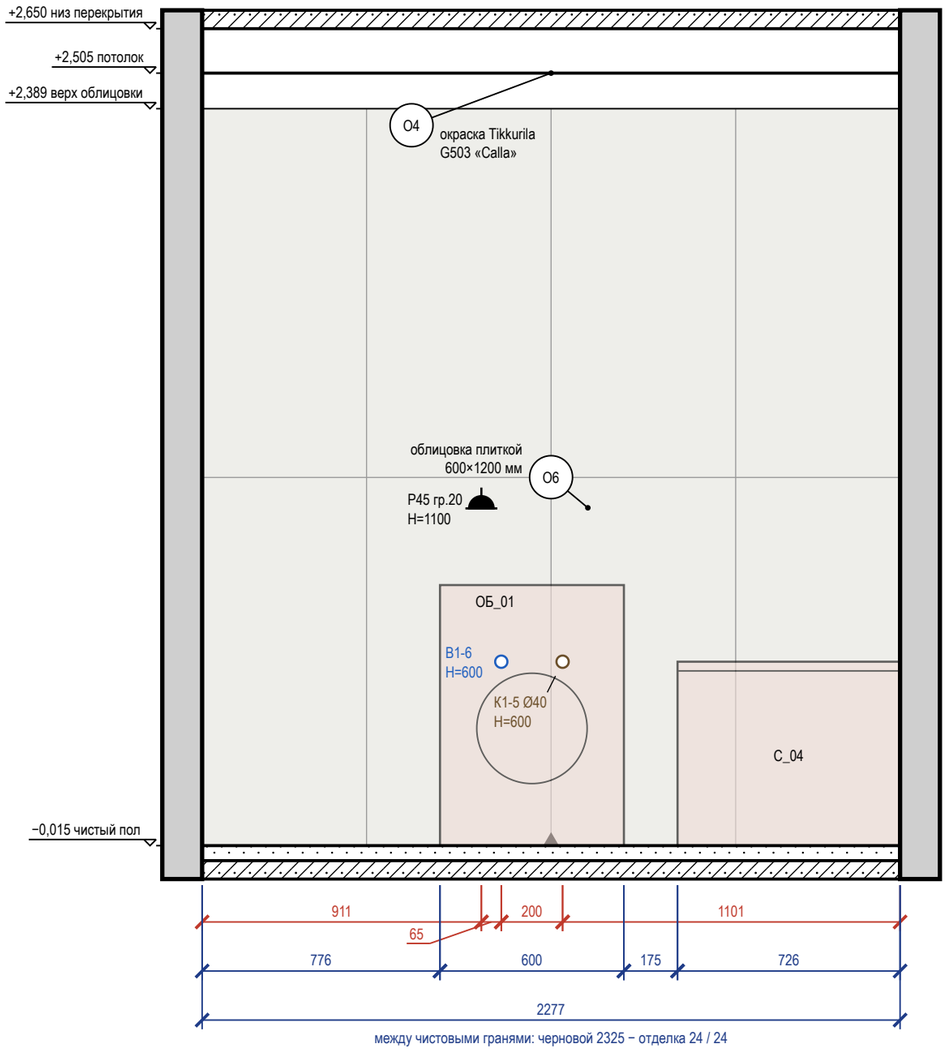


между чистовыми гранями: черновой 2325 − отделка 24 / 24

Развёртка стены Б

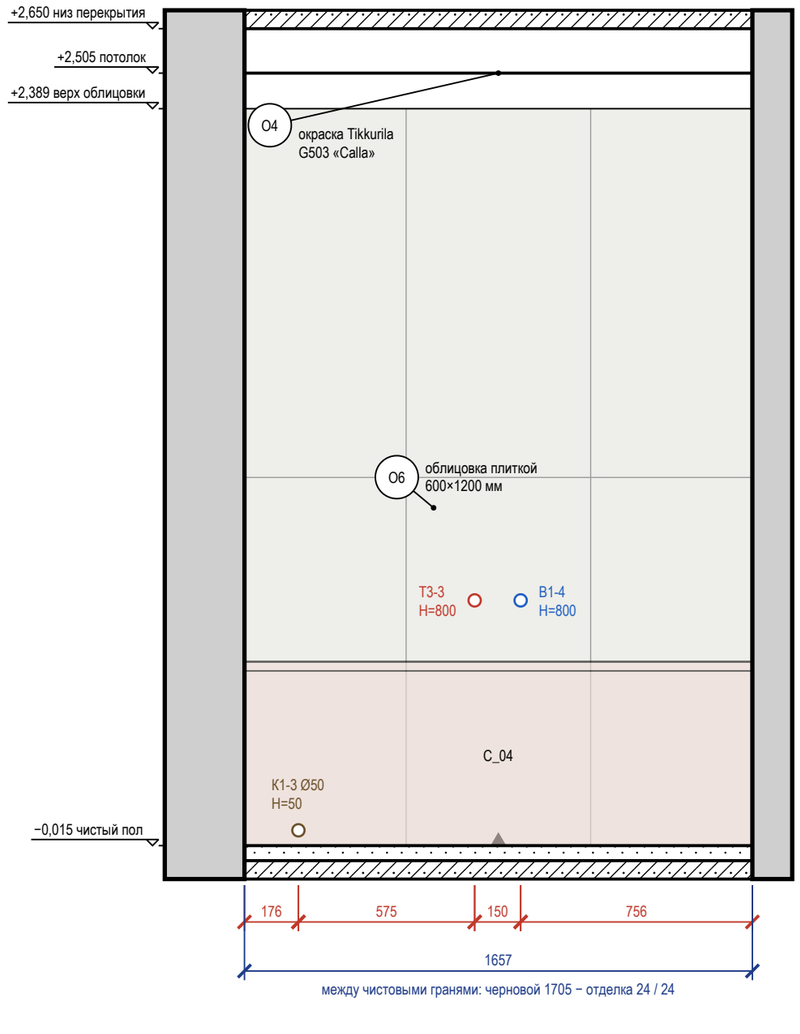

между чистовыми гранями: черновой 1705 − отделка 24 / 24

Схема развёрток (М 1:100)

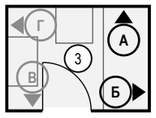

Ведомость отделки (на листе)

Марка	Поверхность	Материал, изделие	Цвет, код	Кол.
О4	потолок	окраска, Tikkurila Euro Power 7, матовая, подготовка Q3	Tikkurila G503 «Calla»	4 м²
О6	стены	облицовка плиткой, 600×1200×9 мм, аналог: керамогранит под травертин, матовый, затирка CG2WA		9,5 м²

Примечания

1. Размеры — в мм от чистовых поверхностей стен; условные обозначения и общие указания — лист 4.
2. Облицовка — по сетке швов 2 мм, раскладка от оси стены (треугольник у пола), целые ряды от пола; подрезки — по листу раскладки плитки.
3. Гидроизоляция в 2 слоя, заход на стены 200 мм; над ванной — до 2000 и 300 мм за борт — до облицовки, с актом скрытых работ и тестом проливом (узел — на листе узлов).


					Проект: Квартира 68 м², элитный модерн — М 1:20
	Лист	№ док.	Подпись	Дата	
Дизайнер	Кырлан А.С.			04.11.26	Развёртки стен А, Б. Ванная (пом. 3)

Стадия	Лист	Листов
П	54	86

выпуск 04.11.2026 № f0db2de63c · стр. 54 из 86


Правка к этому листу

Развёртка стены В

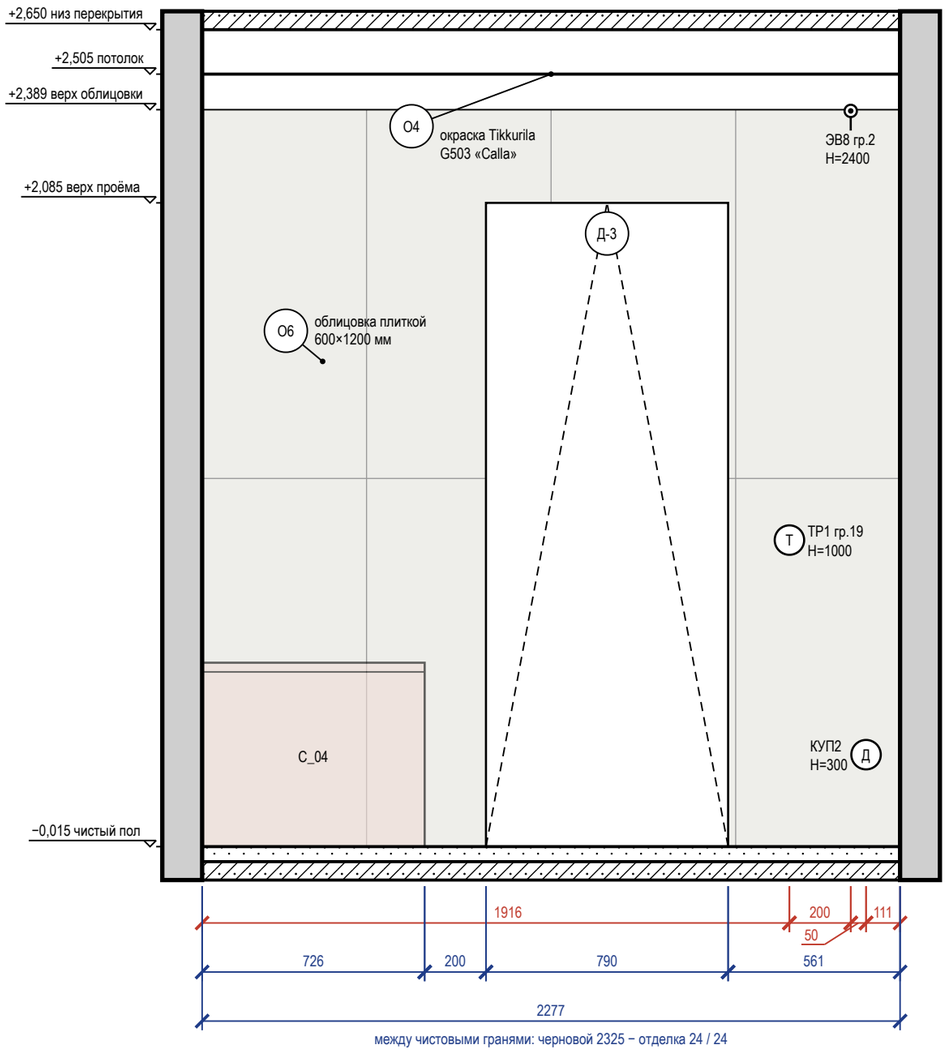


между чистовыми гранями: черновой 2325 − отделка 24 / 24

Развёртка стены Г

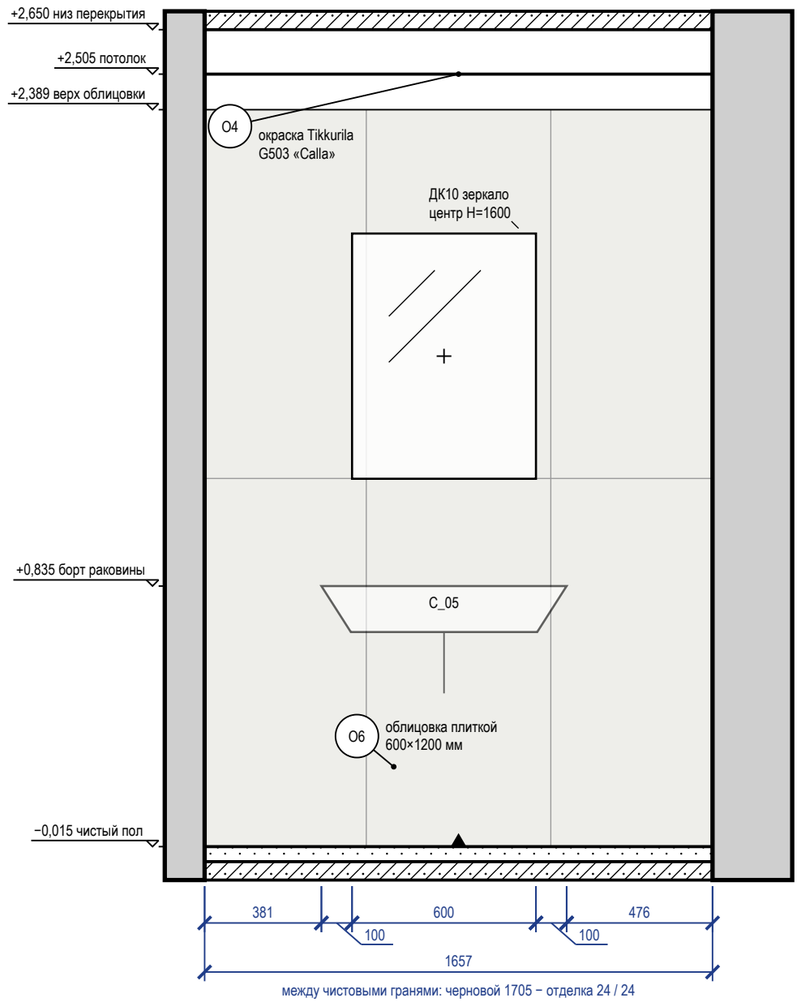

между чистовыми гранями: черновой 1705 − отделка 24 / 24

Схема развёрток (М 1:100)

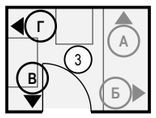

Ведомость отделки (на листе)

Марка	Поверхность	Материал, изделие	Цвет, код	Кол.
О4	потолок	окраска, Tikkurila Euro Power 7, матовая, подготовка Q3	Tikkurila G503 «Calla»	4 м²
О6	стены	облицовка плиткой, 600×1200×9 мм, аналог: керамогранит под травертин, матовый, затирка CG2WA		7,8 м²

Примечания

1. Размеры — в мм от чистовых поверхностей стен; условные обозначения и общие указания — лист 4.
2. Стена Г показана двумя видами: здесь — архитектурная развёртка (мебель, отделка, проёмы, высоты), электроточки и выводы ВК с привязками и таблицей — на листе 56 («Привязки»).
3. Облицовка — по сетке швов 2 мм, раскладка от оси стены (треугольник у пола), целые ряды от пола; подрезки — по листу раскладки плитки.
4. Гидроизоляция в 2 слоя, заход на стены 200 мм; над ванной — до 2000 и 300 мм за борт — до облицовки, с актом скрытых работ и тестом проливом (узел — на листе узлов).
5. Картины и зеркала крепить к основанию по паспорту изделия (закладные и анкеры — в перечне скрытых работ); крест — ось центра предмета.

					Проект: Квартира 68 м², элитный модерн — М 1:20
	Лист	№ док.	Подпись	Дата	
Дизайнер	Кырлан А.С.			04.11.26	Развёртки стен В, Г. Ванная (пом. 3)

Стадия	Лист	Листов
П	55	86

Правка к этому листу

Развёртка стены Г: электроточки и выводы

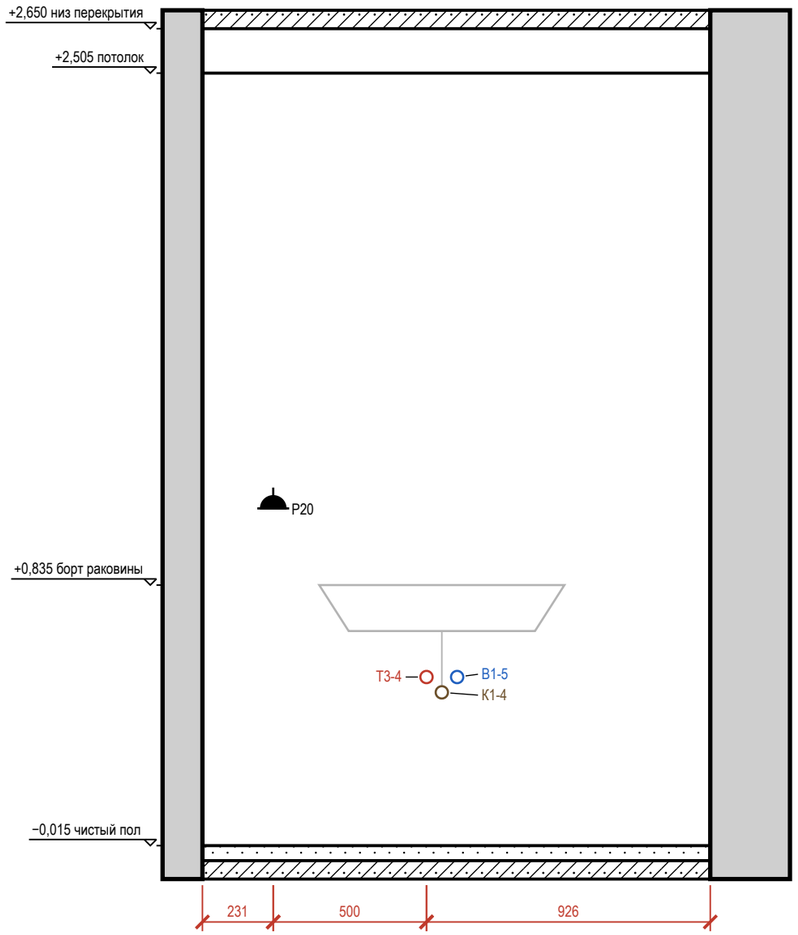



Таблица привязок электроточек и выводов

Марка	Назначение	От угла, мм	Н от пола, мм	Примечание
Р20	розетка: фен у умывальника	231	1100	гр. 15, IP44
Т3-4	горячая вода — умывальник	731	550	межос. 100
К1-4	канализация — умывальник	781	500	Ø40
В1-5	холодная вода — умывальник	831	550	межос. 100

Условные обозначения

- розетка влагозащищённая IP44
- вывод В1 (код — в ведомости привязок)
- вывод Т3 (код — в ведомости привязок)
- вывод К1 (код — в ведомости привязок)
- привязки точек и выводов от угла и от пола, мм
- марка развёртки: буква стены, стрелка — взгляд

Схема развёрток (М 1:50)

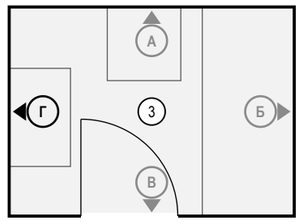

Примечания

1. Вид «Привязки» стены Г — электроточки и выводы ВК; архитектурная развёртка (мебель, отделка, проёмы, высоты) — на листе 55. Мебель и приборы — подложкой для ориентира; их марки и обозначения мебели, проёмов и стен — там же.
2. Привязки — в мм: по горизонтали от левого чистового угла стены до оси изделия, Н — от чистого пола до оси; все точки — в таблице привязок. Красная цепочка — привязки по осям; точки ближе 120 мм одна к другой в цепочку не дробятся — их привязки только в таблице.
3. У знака — марка электроточки (Р — розетка, S — выключатель, Св — светильник, ЭВ — вывод кабеля); условные обозначения и общие указания — лист 4.
4. Коды выводов ВК: В1 — холодная вода, Т3 — горячая вода, К1 — канализация; номер после дефиса — номер вывода на листе выводов сантехники.

					Проект: Квартира 68 м², элитный модерн	М 1:20
	Лист	№ док.	Подпись	Дата	Привязки электроточек и выводов ВК, стена Г. Ванная (пом. 3)	Стадия / Лист / Листов
Дизайнер	Кырлан А.С.			04.11.26		П / 56 / 86

выпуск 04.11.2026 № f0db2de63c · стр. 56 из 86

Правка к этому листу

Развёртка стены А


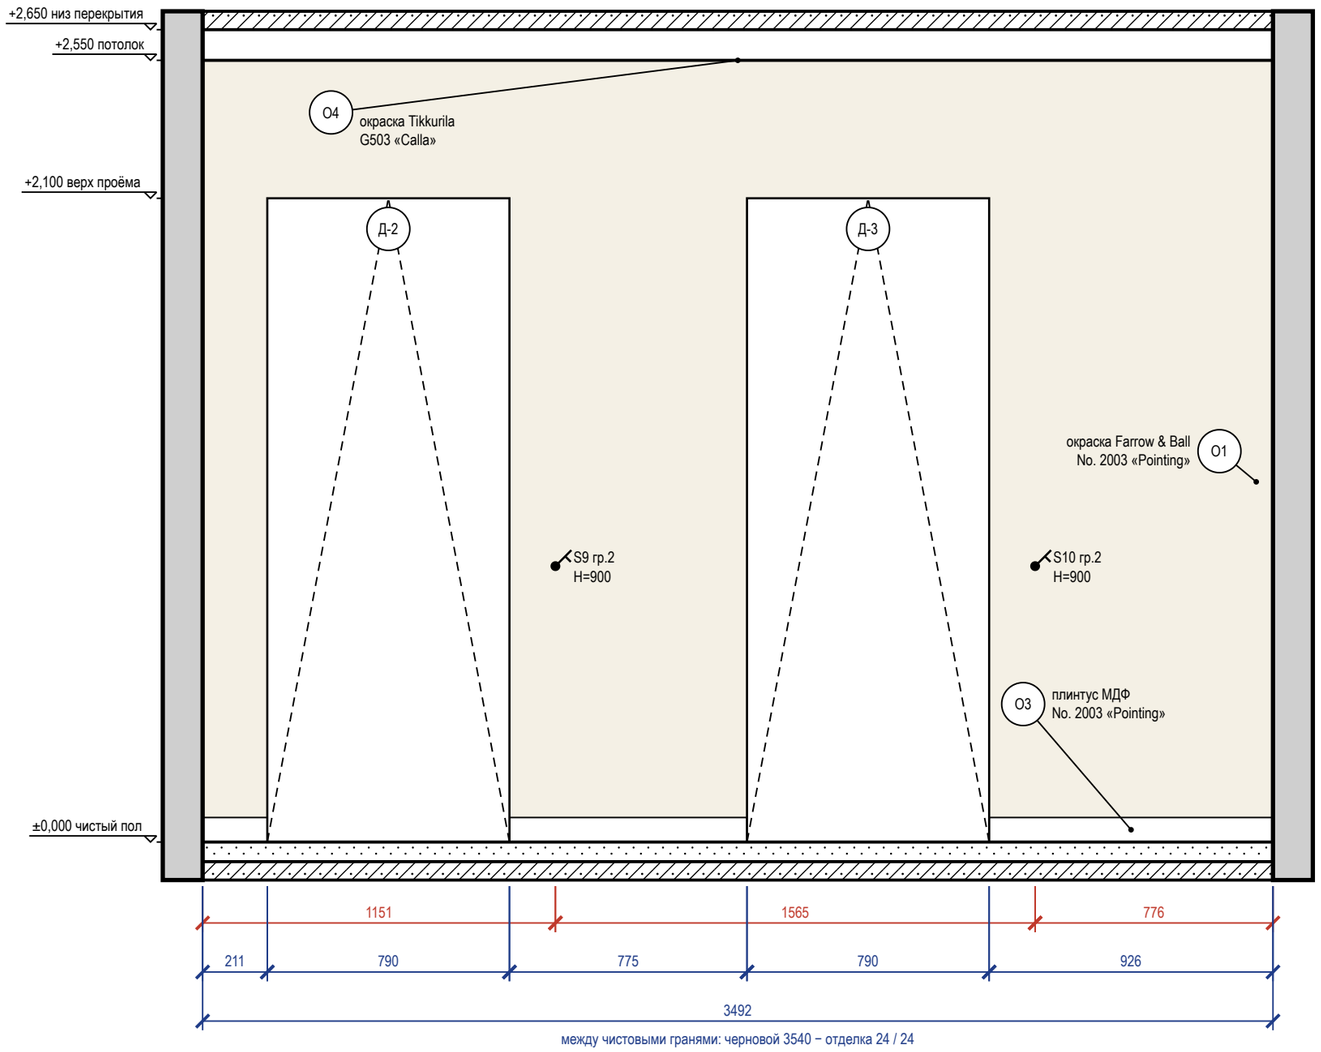


Схема развёрток (М 1:100)

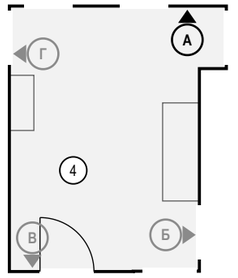

Ведомость отделки (на листе)

Марка	Поверхность	Материал, изделие	Цвет, код	Кол.
О1	стены	окраска, Farrow & Ball Modern Emulsion, матовая, подготовка Q3	Farrow & Ball No. 2003 «Pointing»	5,6 м²
О3	плинтус	плинтус МДФ, h 80 мм, аналог: плинтус МДФ под покраску 80×16	Farrow & Ball No. 2003 «Pointing»	1,9 м
О4	потолок	окраска, Tikkurila Euro Power 7, глубокоматовая, подготовка Q3	Tikkurila G503 «Calla»	13,9 м²

Примечания

1. Размеры — в мм от чистовых поверхностей стен; условные обозначения и общие указания — лист 4.
2. Потолок — у каждой стены свой, по плану потолков (ПТ3); ступени — зоной, кромка короба перед нишей — тонкой линией; в поле потолка: ПТ4 +2,650.

					Проект: Квартира 68 м², элитный модерн — М 1:20
	Лист	№ док.	Подпись	Дата	
Дизайнер	Кырлан А.С.			04.11.26	Развёртка стены А. Прихожая (пом. 4)

Стадия	Лист	Листов
П	57	86

Правка к этому листу

Развёртка стены Б


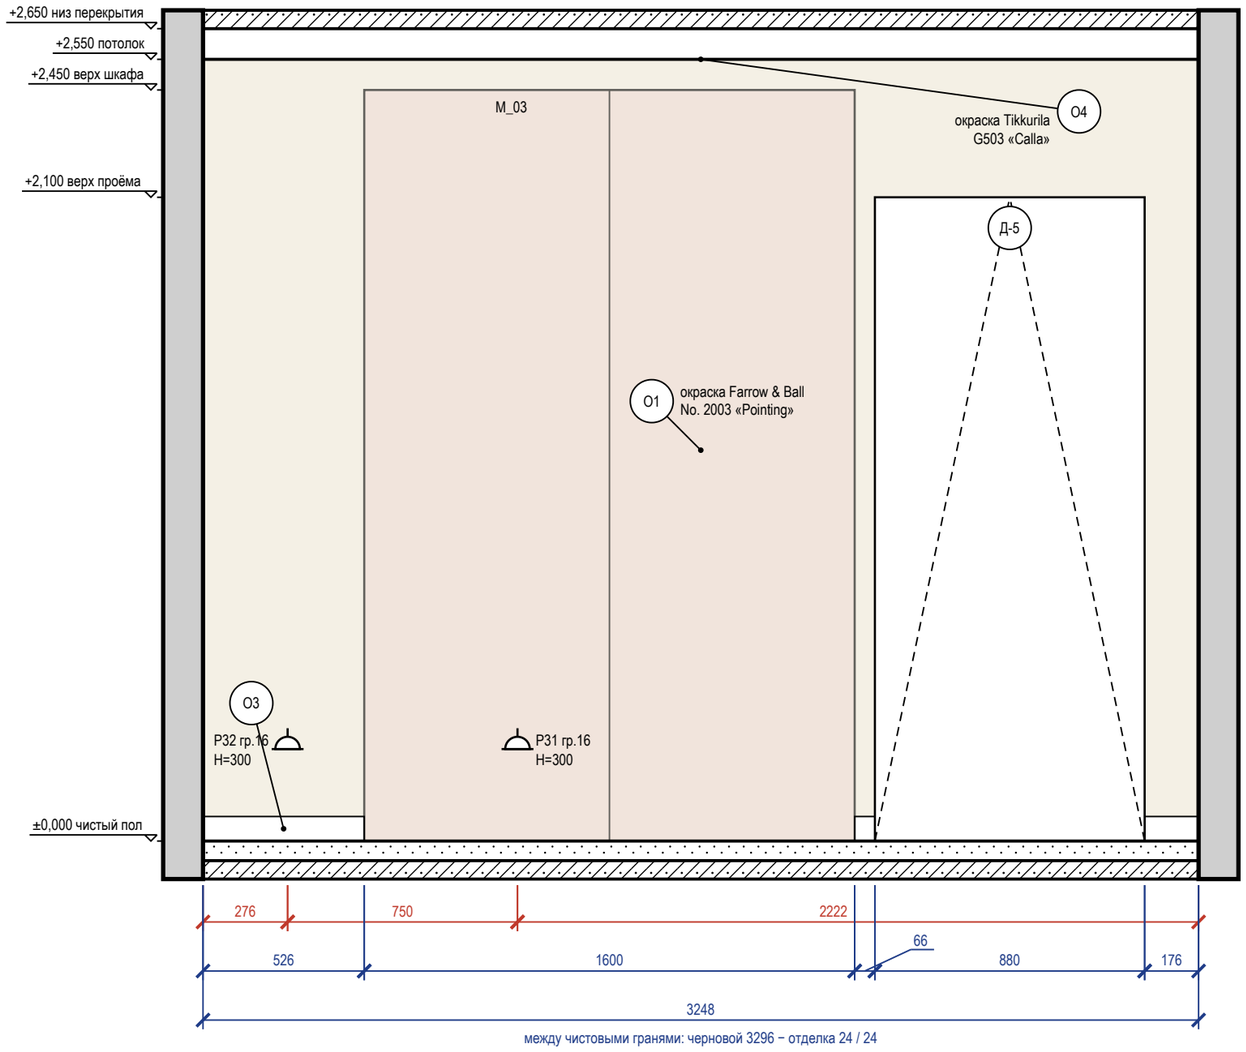


Схема развёрток (М 1:100)

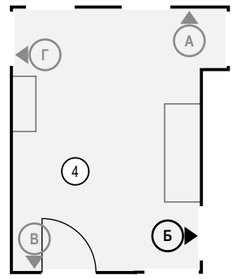

Ведомость отделки (на листе)

Марка	Поверхность	Материал, изделие	Цвет, код	Кол.
О1	стены	окраска, Farrow & Ball Modern Emulsion, матовая, подготовка Q3	Farrow & Ball No. 2003 «Pointing»	6,4 м²
О3	плинтус	плинтус МДФ, h 80 мм, аналог: плинтус МДФ под покраску 80×16	Farrow & Ball No. 2003 «Pointing»	0,8 м
О4	потолок	окраска, Tikkurila Euro Power 7, глубокоматовая, подготовка Q3	Tikkurila G503 «Calla»	13,9 м²

Примечания

1. Размеры — в мм от чистовых поверхностей стен; условные обозначения и общие указания — лист 4.
2. Потолок — у каждой стены свой, по плану потолков (ПТ3); ступени — зоной, кромка короба перед нишей — тонкой линией; в поле потолка: ПТ4 +2,650.

					Проект: Квартира 68 м², элитный модерн — М 1:20
	Лист	№ док.	Подпись	Дата	Развёртка стены Б. Прихожая (пом. 4)
Дизайнер	Кырлан А.С.			04.11.26	

Стадия	Лист	Листов
П	58	86

Развёртка стены В


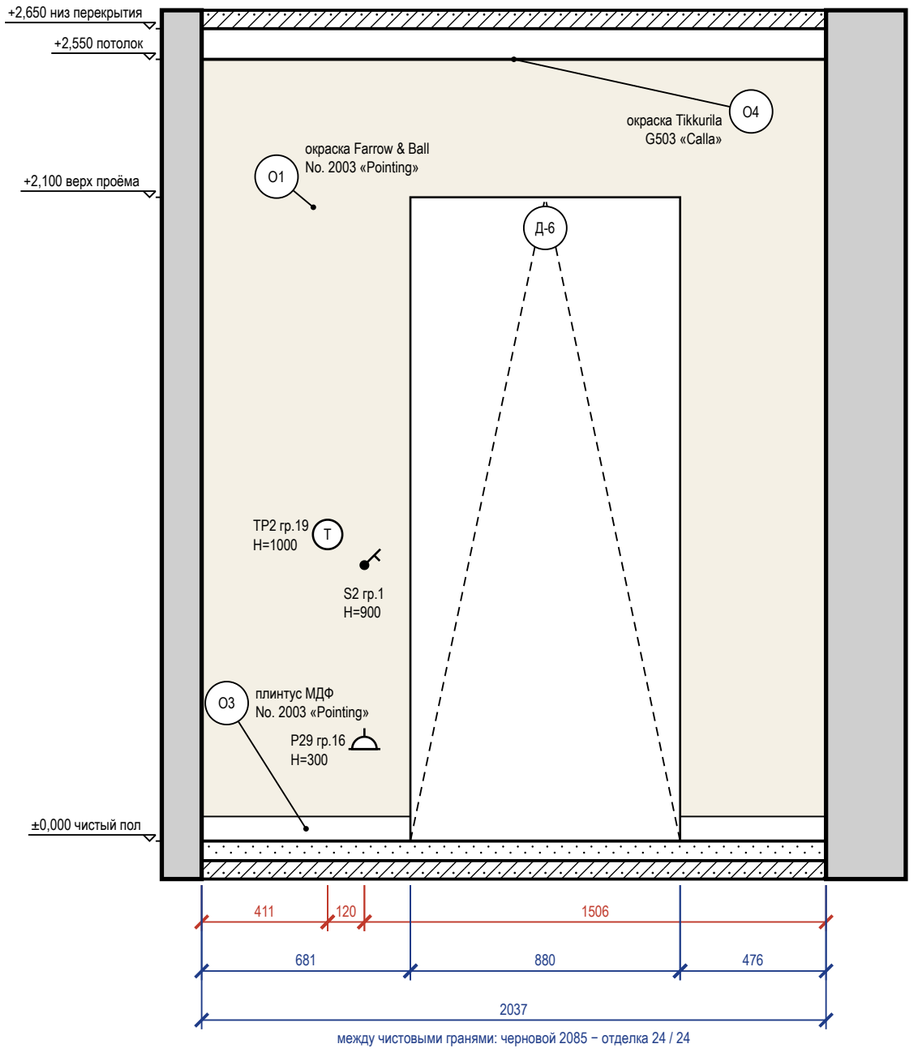


Схема развёрток (М 1:100)

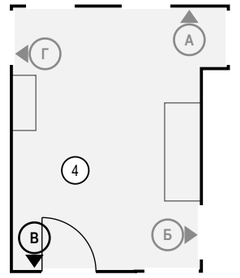


Ведомость отделки (на листе)

Марка	Поверхность	Материал, изделие	Цвет, код	Кол.
О1	стены	окраска, Farrow & Ball Modern Emulsion, матовая, подготовка Q3	Farrow & Ball No. 2003 «Pointing»	3,3 м²
О3	плинтус	плинтус МДФ, h 80 мм, аналог: плинтус МДФ под покраску 80×16	Farrow & Ball No. 2003 «Pointing»	1,2 м
О4	потолок	окраска, Tikkurila Euro Power 7, глубокоматовая, подготовка Q3	Tikkurila G503 «Calla»	13,9 м²

5 **Плинтус МДФ 80×16 мм у окрашенной стены по керамограниту (плитке) (М 1:10)**

Узел 5 — лист С6

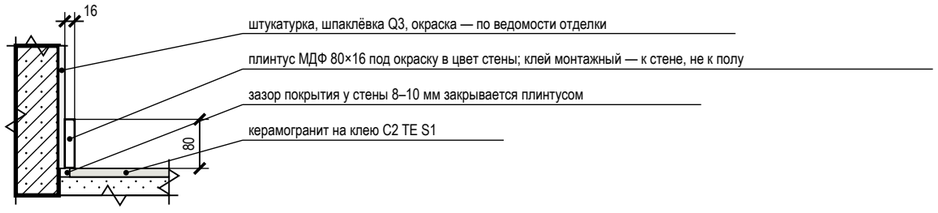

Примечания

1. Размеры — в мм от чистовых поверхностей стен; условные обозначения и общие указания — лист 4.
2. Потолок — у каждой стены свой, по плану потолков (ПТ3); ступени — зоной, кромка короба перед нишей — тонкой линией; в поле потолка: ПТ4 +2,650.

					Проект: Квартира 68 м², элитный модерн	М 1:20
	Лист	№ док.	Подпись	Дата		
Дизайнер	Кырлан А.С.			04.11.26	Развёртка стены В. Прихожая (пом. 4)	Стадия: П; Лист: 59; Листов: 86

выпуск 04.11.2026 № f0db2de63c · стр. 59 из 86

Развёртка стены Г


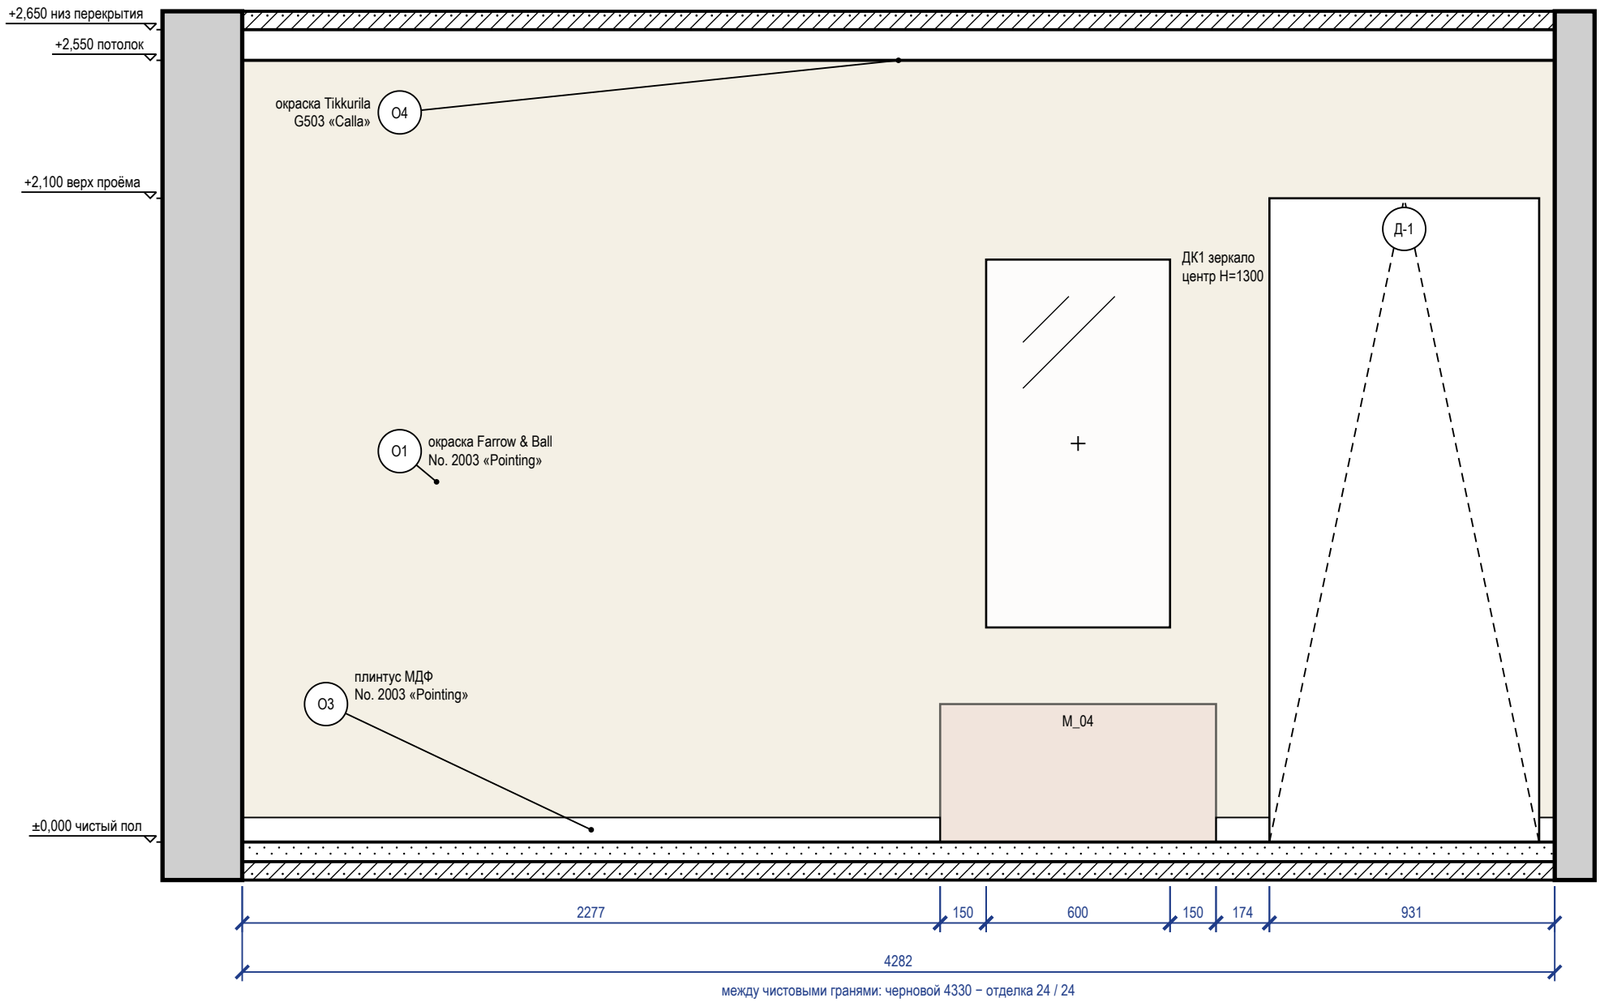


Схема развёрток (М 1:100)

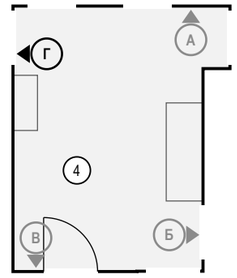

Ведомость отделки (на листе)

Марка	Поверхность	Материал, изделие	Цвет, код	Кол.
O1	стены	окраска, Farrow & Ball Modern Emulsion, матовая, подготовка Q3	Farrow & Ball No. 2003 «Pointing»	9,1 м²
O3	плинтус	плинтус МДФ, h 80 мм, аналог: плинтус МДФ под покраску 80×16	Farrow & Ball No. 2003 «Pointing»	2,5 м
O4	потолок	окраска, Tikkurila Euro Power 7, глубокоматовая, подготовка Q3	Tikkurila G503 «Calla»	13,9 м²

Примечания

1. Размеры — в мм от чистовых поверхностей стен; условные обозначения и общие указания — лист 4.
2. Стена Г показана двумя видами: здесь — архитектурная развёртка (мебель, отделка, проёмы, высоты), электроточки и выводы ВК с привязками и таблицей — на листе 61 («Привязки»).
3. Картины и зеркала крепить к основанию по паспорту изделия (закладные и анкеры — в перечне скрытых работ); крест — ось центра предмета.
4. Потолок — у каждой стены свой, по плану потолков (ПТ3); ступени — зоной, кромка короба перед нишей — тонкой линией; в поле потолка: ПТ4 +2,650.

					Проект: Квартира 68 м², элитный модерн	М 1:20
	Лист	№ док.	Подпись	Дата	Развёртка стены Г. Прихожая (пом. 4)	Стадия: П; Лист: 60; Листов: 86
Дизайнер	Кырлан А.С.			04.11.26		

Развёртка стены Г: электроточки и выводы

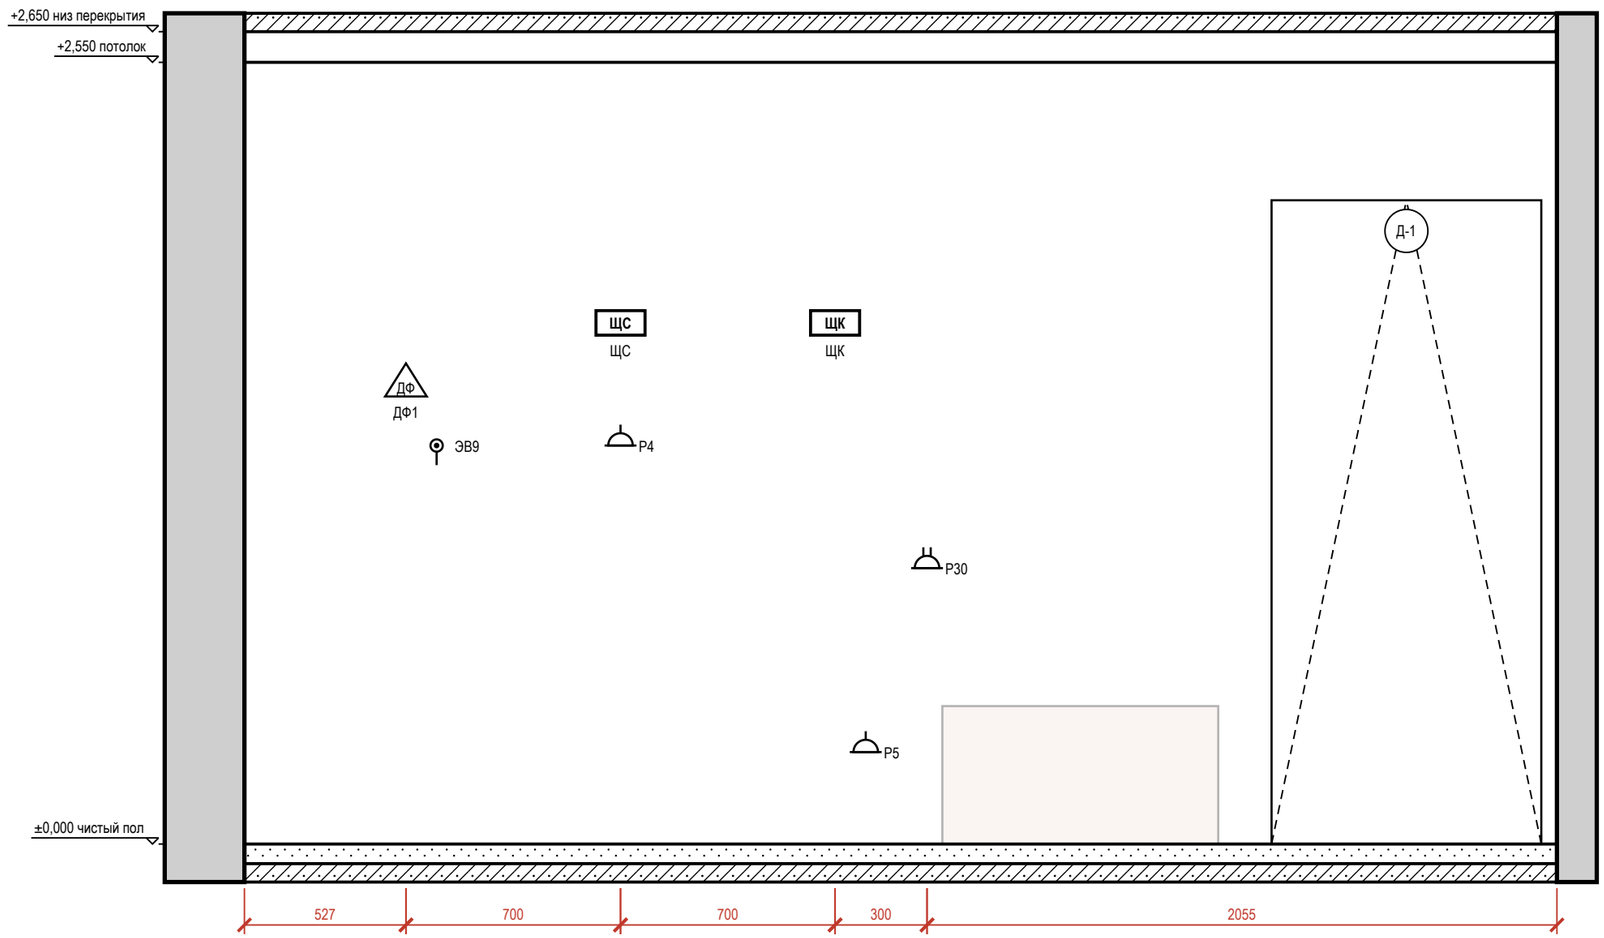



Таблица привязок электроточек и выводов

Марка	Назначение	От угла, мм	Н от пола, мм	Примечание
ДФ1	домофон: трубка домофона	527	1500	
ЭВ9	вывод кабеля: контроллер защиты от протечек и питание электрокранов (у слаботочного щита)	627	1300	гр. 16
Р4	розетка: питание слаботочного щита (роутер, ONT)	1227	1300	гр. 16
ЩС	щит: щит слаботочный: ввод провайдера, ONT, роутер	1227	1700	
ЩК	щит: щит квартирный ЩРВ-П-72, IP41	1927	1700	
Р5	розетка: уборка, сушилка обуви	2027	300	гр. 7
Р30	розетка: прихожая: зарядка телефона и ключей	2227	900	рамка 2 поста, гр. 16

Условные обозначения

- розетка с заземляющим контактом; у знака — марка, ×N постов в рамке, гр. — группа щита, Н — высота оси, мм
- вывод кабеля для подключения прибора (без розетки), марка ЭВ
- ДФ — трубка или монитор домофона
- ЩК — щит квартирный
- привязки точек и выводов от угла и от пола, мм
- А — марка развёртки: буква стены, стрелка — взгляд

Схема развёрток (М 1:100)

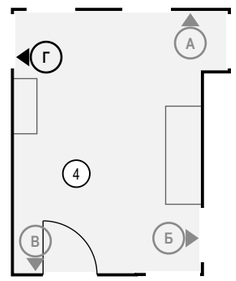

Примечания

1. Вид «Привязки» стены Г — электроточки и выводы ВК; архитектурная развёртка (мебель, отделка, проёмы, высоты) — на листе 60. Мебель и приборы — подложкой для ориентира; их марки и обозначения мебели, проёмов и стен — там же.
2. Привязки — в мм: по горизонтали от левого чистового угла стены до оси изделия, Н — от чистого пола до оси; все точки — в таблице привязок. Красная цепочка — привязки по осям; точки ближе 120 мм одна к другой в цепочку не дробятся — их привязки только в таблице.
3. У знака — марка электроточки (Р — розетка, S — выключатель, Св — светильник, ЭВ — вывод кабеля); условные обозначения и общие указания — лист 4.

					Проект: Квартира 68 м², элитный модерн	М 1:20
	Лист	№ док.	Подпись	Дата	Привязки электроточек, стена Г. Прихожая (пом. 4)	Стадия / Лист / Листов
Дизайнер	Кырлан А.С.			04.11.26		П / 61 / 86

Правка к этому листу

Развёртка стены А1


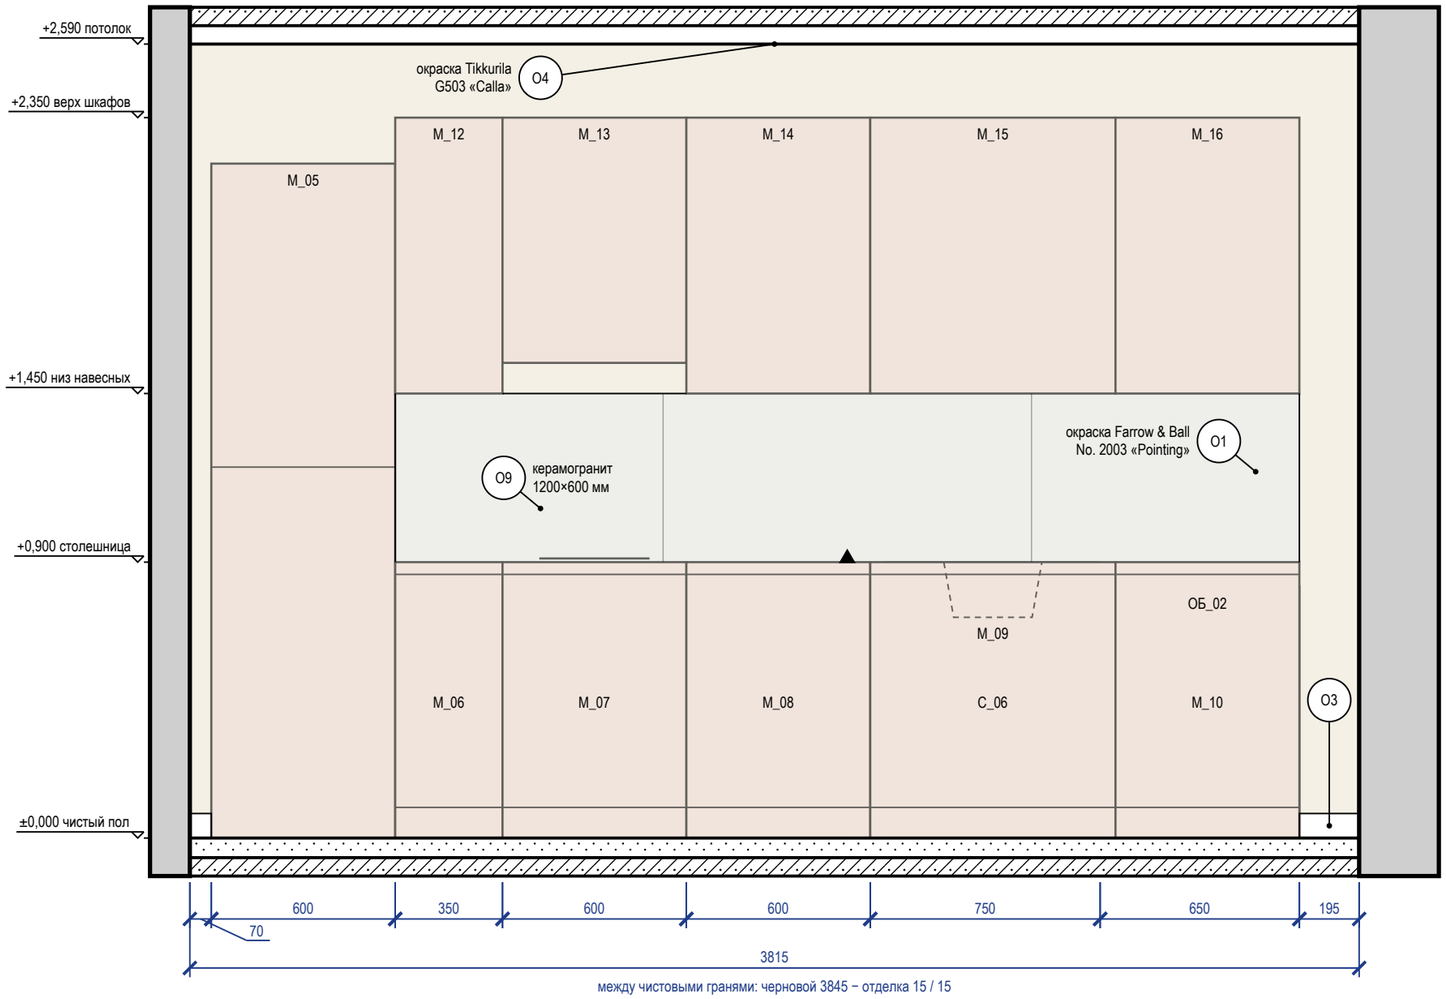


Схема развёрток (М 1:100)

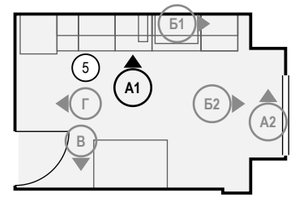

Ведомость отделки (на листе)

Марка	Поверхность	Материал, изделие	Цвет, код	Кол.
О1	стены	окраска, Farrow & Ball Modern Emulsion, матовая, подготовка Q3	Farrow & Ball No. 2003 «Pointing»	8,3 м²
О3	плинтус	плинтус МДФ, h 80 мм, аналог: плинтус МДФ под покраску 80×16	Farrow & Ball No. 2003 «Pointing»	0,3 м
О4	потолок	окраска, Tikkurila Euro Power 7, глубокоматовая, подготовка Q3	Tikkurila G503 «Calla»	12 м²
О9	фартук	керамогранит, 1200×600×9 мм, аналог: керамогранит под травертин, матовый, затирка CG2WA		1,6 м²

Примечания

1. Размеры — в мм от чистовых поверхностей стен; условные обозначения и общие указания — лист 4.
2. Стена А1 показана двумя видами: здесь — архитектурная развёртка (мебель, отделка, проёмы, высоты), электроточки и выводы ВК с привязками и таблицей — на листе 63 («Привязки»).
3. Схема мебели, приборов и декора не является технической документацией для производства мебели; габариты — по паспортам изделий.

					Проект: Квартира 68 м², элитный модерн	М 1:20
	Лист	№ док.	Подпись	Дата	Развёртка стены А1. Кухня-столовая (пом. 5), кухонный фронт	Стадия / Лист / Листов
Дизайнер	Кырлан А.С.			04.11.26		П / 62 / 86

Правка к этому листу

Развёртка стены А1: электроточки и выводы

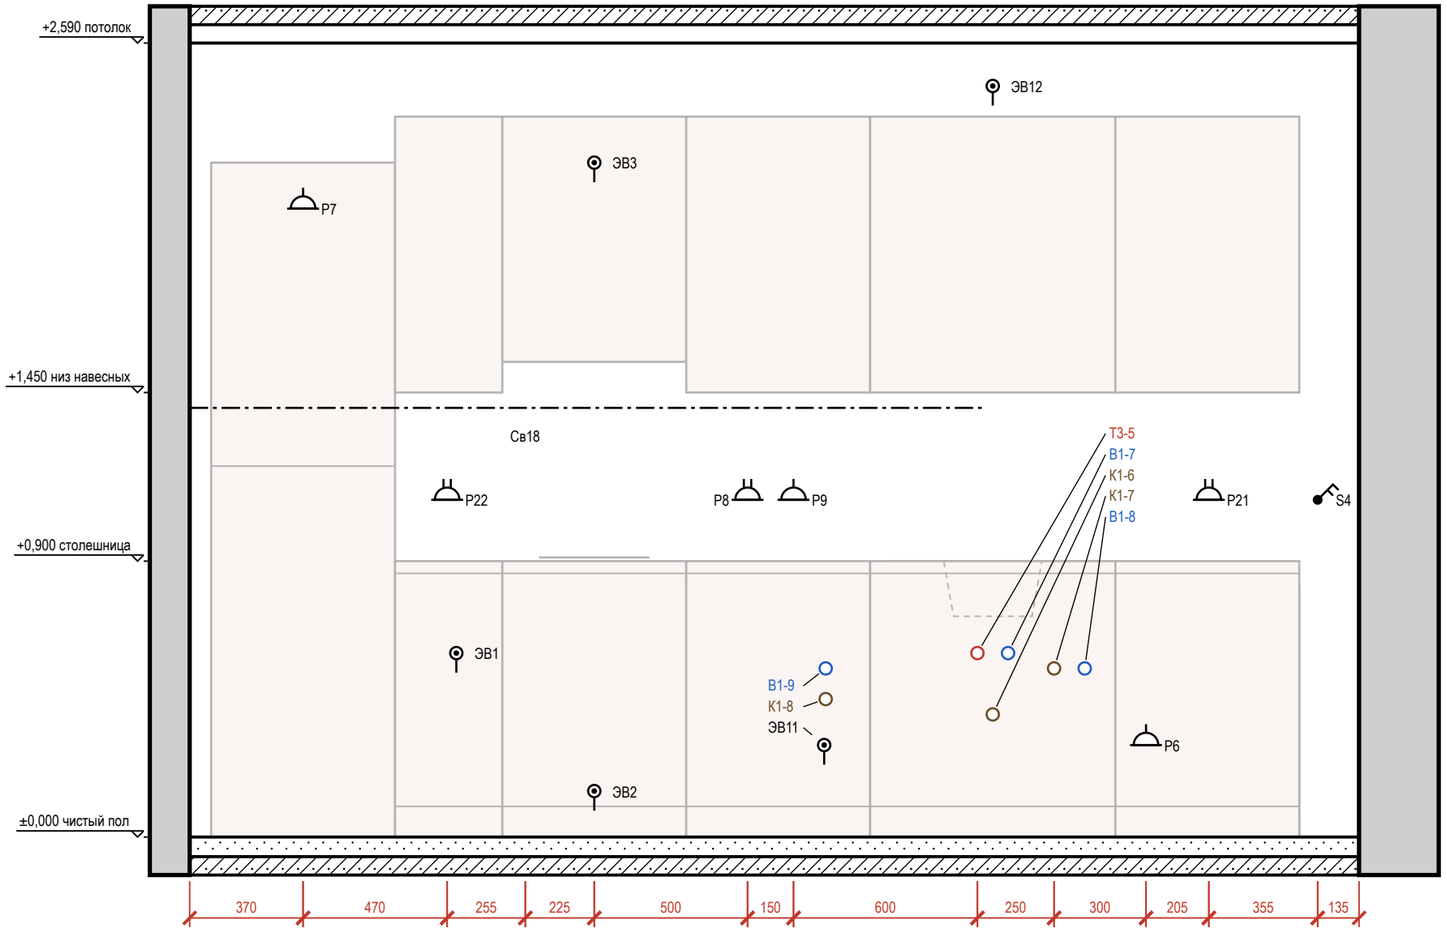


Таблица привязок электроточек и выводов

Марка	Назначение	От угла, мм	Н от пола, мм	Примечание
Р7	розетка: холодильник — над нишей, съёмная панель	370	2050	гр. 10
Р22	розетка: фартук	840	1100	рамка 2 поста, гр. 8
ЭВ1	вывод кабеля: варочная панель — в соседнем модуле, за ящиком	870	600	гр. 12
Св18	светильник настенный: марка 13 по исходному плану: «підсвітка робочої поверхні»	1095	1400	гр. 1, лента -405–2595 от угла
ЭВ2	вывод кабеля: духовой шкаф — в цоколе	1320	150	гр. 13
ЭВ3	вывод кабеля: вытяжка — над корпусом	1320	2200	гр. 11
Р8	розетка: чайник и кофемашина (отдельная линия)	1820	1100	рамка 2 поста, гр. 9
Р9	розетка: фартук: мелкая техника	1970	1100	гр. 8
ЭВ11	вывод кабеля: измельчитель мойки	2070	300	гр. 8
К1-8	канализация — фильтр обратного осмоса	2075	450	Ø40
В1-9	холодная вода — фильтр обратного осмоса	2075	550	
Т3-5	горячая вода — мойка кухонная	2570	600	межос. 100
К1-6	канализация — мойка кухонная	2620	400	Ø50
ЭВ12	вывод кабеля: подсветка навесных шкафов (блок питания ленты)	2620	2450	гр. 8
В1-7	холодная вода — мойка кухонная	2670	600	межос. 100
К1-7	канализация — посудомоечная машина	2820	550	Ø40; слив ПММ в шкафу мойки
В1-8	холодная вода — посудомоечная машина	2920	550	кран ПММ в шкафу мойки
Р6	розетка: посудомоечная машина (в нише М_10, сбоку от корпуса, доступ через цоколь)	3120	300	гр. 14
Р21	розетка: фартук	3325	1100	рамка 2 поста, гр. 8
S4	выключатель	3680	1100	гр. 1

Условные обозначения

- розетка с заземляющим контактом; у знака — марка, ×N постов в рамке, гр. — группа щита, Н — высота оси, мм
- вывод кабеля для подключения прибора (без розетки), марка ЭВ
- выключатель одноклавишный
- выключатель двухклавишный (флажков — по числу клавиш)
- светодиодная лента в профиле / в карнизе короба
- вывод В1 (код — в ведомости привязок)
- вывод Т3 (код — в ведомости привязок)
- вывод К1 (код — в ведомости привязок)
- привязки точек и выводов от угла и от пола, мм

Примечания


1. Вид «Привязки» стены А1 — электроточки и выводы ВК; архитектурная развёртка (мебель, отделка, проёмы, высоты) — на листе 62. Мебель и приборы — подложкой для ориентира; их марки и обозначения мебели, проёмов и стен — там же.
2. Привязки — в мм: по горизонтали от левого чистового угла стены до оси изделия, Н — от чистого пола до оси; все точки — в таблице привязок. Красная цепочка — привязки по осям; точки ближе 120 мм одна к другой в цепочку не дробятся — их привязки только в таблице.
3. У знака — марка электроточки (Р — розетка, S — выключатель, Св — светильник, ЭВ — вывод кабеля); условные обозначения и общие указания — лист 4.
4. Коды выводов ВК: В1 — холодная вода, Т3 — горячая вода, К1 — канализация; номер после дефиса — номер вывода на листе выводов сантехники.
5. Выводы кухонной техники — по утверждённому проекту кухни: привязки выводов даются от осей модулей гарнитура.

					Проект: Квартира 68 м², элитный модерн — М 1:20
	Лист	№ док.	Подпись	Дата	
Дизайнер	Кырлан А.С.			04.11.26	Привязки электроточек и выводов ВК, стена А1. Кухня-столовая (пом. 5)

Стадия	Лист	Листов
П	63	86


Правка к этому листу

Развёртка стены А2

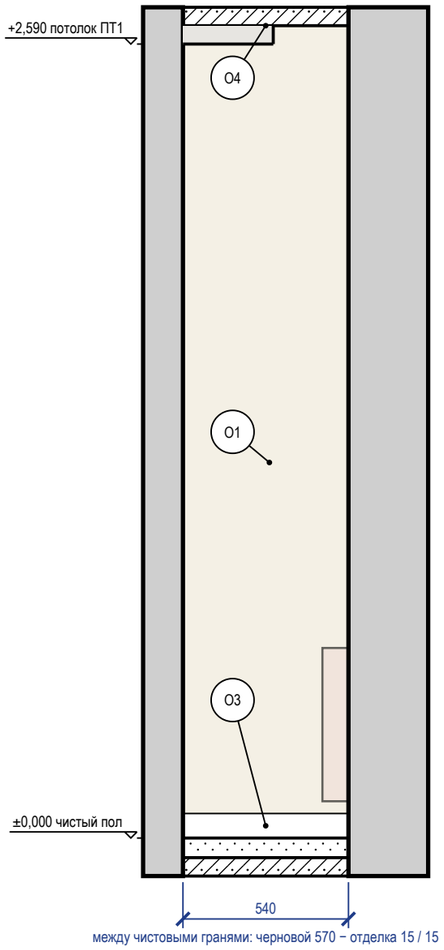


между чистовыми гранями: черновой 570 − отделка 15 / 15

Развёртка стены Б1

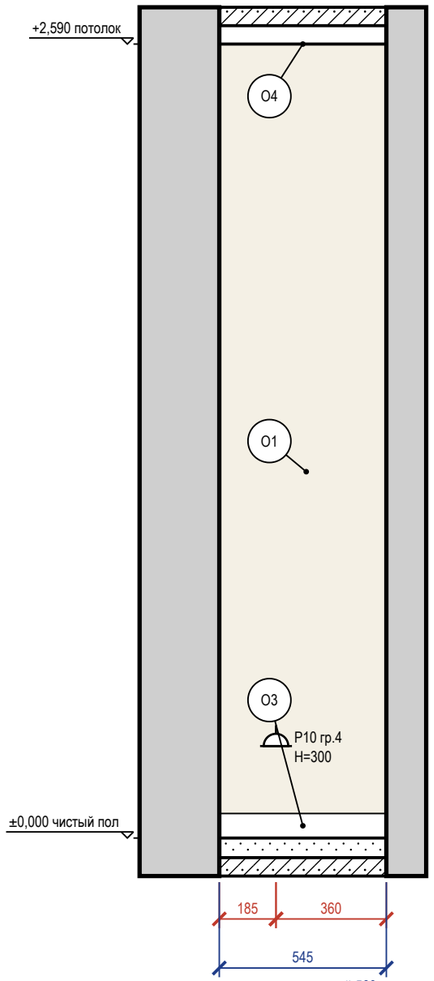


между чистовыми гранями: черновой 560 − отделка 15 / 0

Развёртка стены Б2

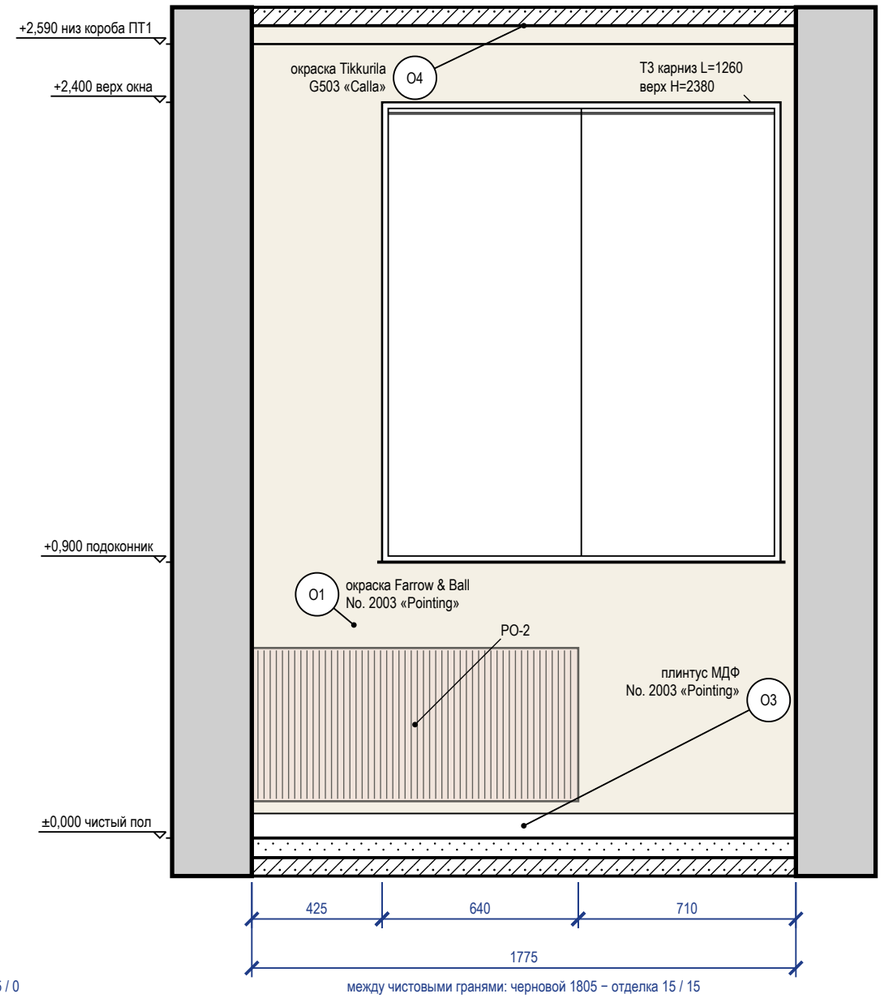

между чистовыми гранями: черновой 1805 − отделка 15 / 15

Схема развёрток (М 1:100)

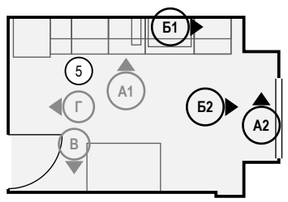

Ведомость отделки (на листе)

Марка	Поверхность	Материал, изделие	Цвет, код	Кол.
О1	стены	окраска, Farrow & Ball Modern Emulsion, матовая, подготовка Q3	Farrow & Ball No. 2003 «Pointing»	5,6 м²
О3	плинтус	плинтус МДФ, h 80 мм, аналог: плинтус МДФ под покраску 80×16	Farrow & Ball No. 2003 «Pointing»	2,9 м
О4	потолок	окраска, Tikkurila Euro Power 7, глубокоматовая, подготовка Q3	Tikkurila G503 «Calla»	12 м²

Примечания

1. Размеры — в мм от чистовых поверхностей стен; условные обозначения и общие указания — лист 4.
2. Карнизы (шины) — по ведомости текстиля декоратора: длина L и верх H на развёртке — те же числа, что в ведомости; крепление — до окраски потолка.

	Лист	№ док.	Подпись	Дата
Дизайнер	Кырлан А.С.			04.11.26

Проект: Квартира 68 м², элитный модерн — **М 1:20**

Развёртки стен А2, Б1, Б2.
Кухня-столовая (пом. 5)

Стадия	Лист	Листов
П	64	86

выпуск 04.11.2026 № f0db2de63c · стр. 64 из 86

Правка к этому листу

Развёртка стены В


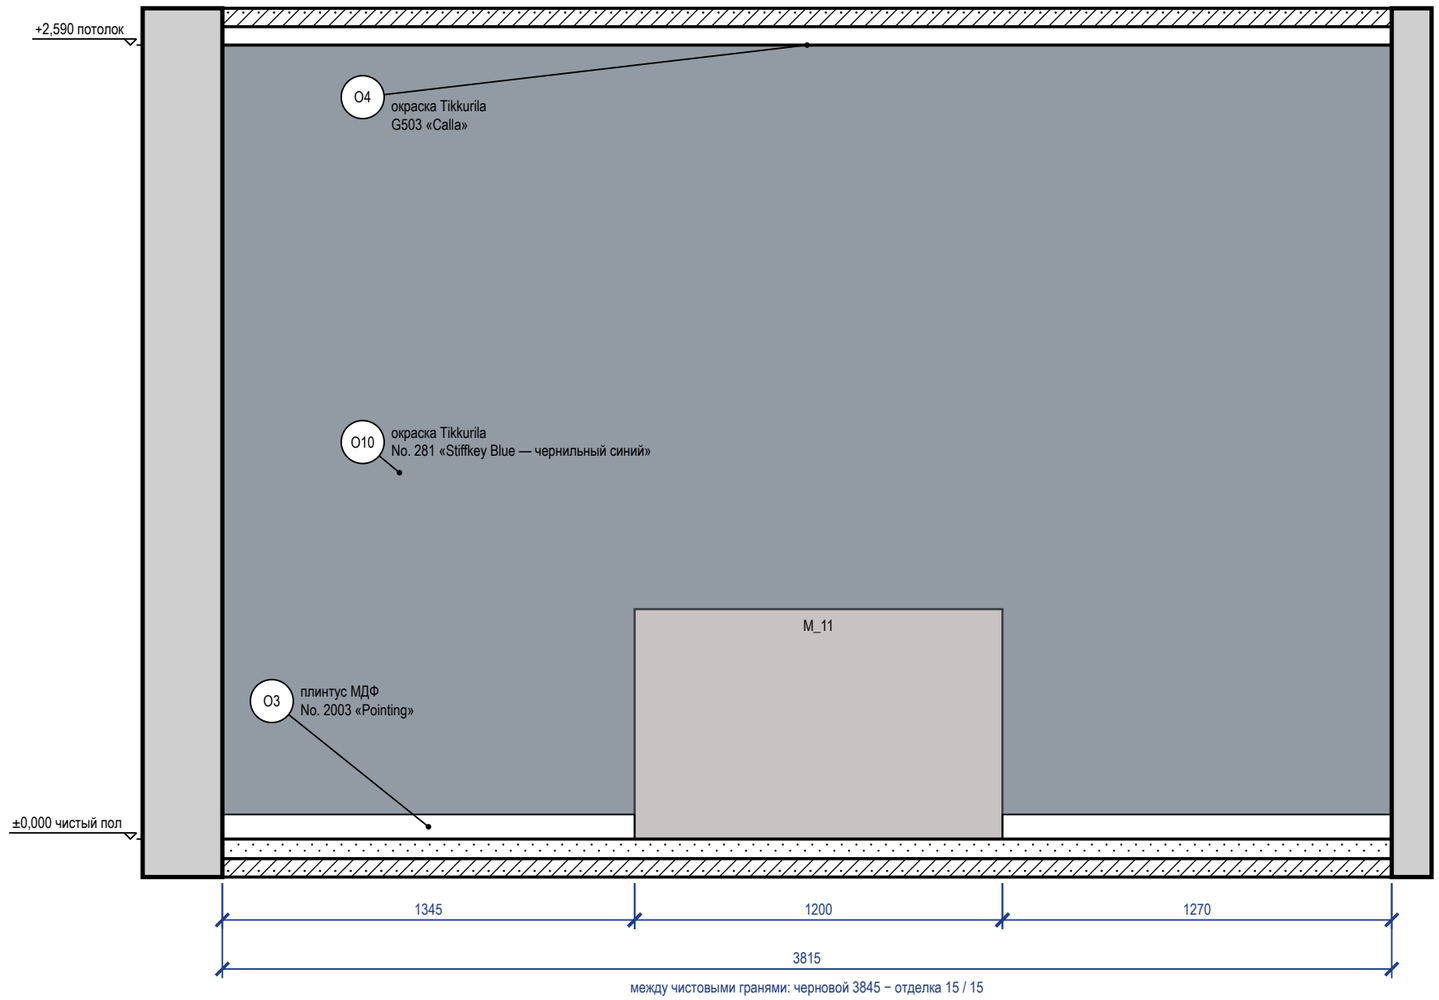


Схема развёрток (М 1:100)

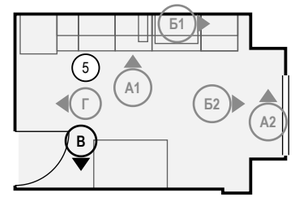

Ведомость отделки (на листе)

Марка	Поверхность	Материал, изделие	Цвет, код	Кол.
О3	плинтус	плинтус МДФ, h 80 мм, аналог: плинтус МДФ под покраску 80×16	Farrow & Ball No. 2003 «Pointing»	2,6 м
О4	потолок	окраска, Tikkurila Euro Power 7, глубокоматовая, подготовка Q3	Tikkurila G503 «Calla»	12 м²
О10	акцентная стена	окраска, Tikkurila Euro Power 7, колеровка по NCS, матовая, подготовка Q3	Farrow & Ball No. 281 «Stiffkey Blue — чернильный синий»	9,9 м²

Примечания

1. Размеры — в мм от чистовых поверхностей стен; условные обозначения и общие указания — лист 4.

	Лист	№ док.	Подпись	Дата
Дизайнер	Кырлан А.С.			04.11.26

Проект: Квартира 68 м², элитный модерн — **М 1:20**

Развёртка стены В. Кухня-столовая (пом. 5)

Стадия	Лист	Листов
П	65	86

Правка к этому листу

Развёртка стены Г


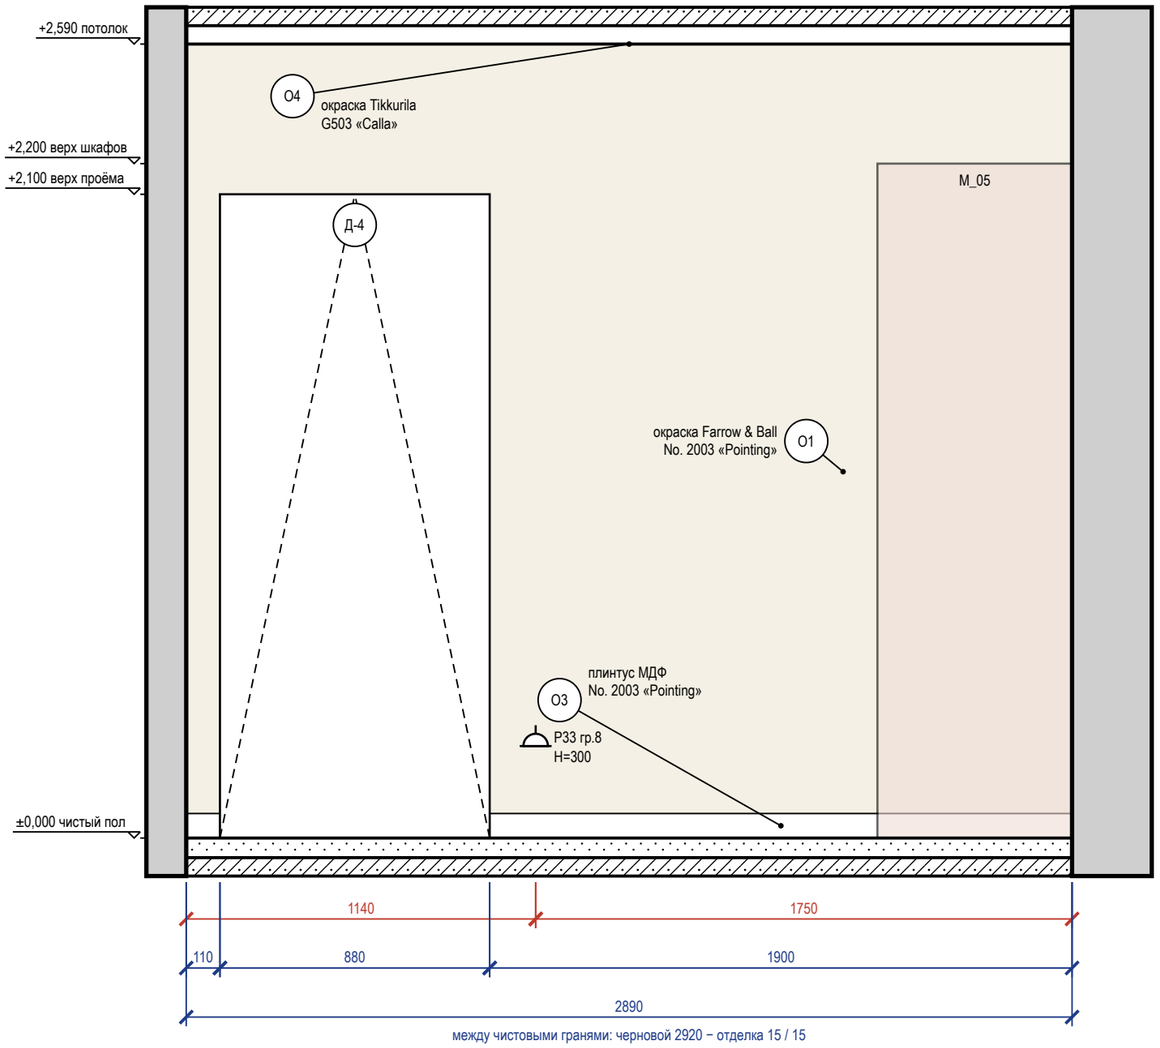


Схема развёрток (М 1:100)

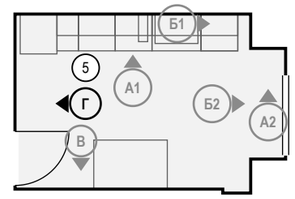

Ведомость отделки (на листе)

Марка	Поверхность	Материал, изделие	Цвет, код	Кол.
О1	стены	окраска, Farrow & Ball Modern Emulsion, матовая, подготовка Q3	Farrow & Ball No. 2003 «Pointing»	5,6 м²
О3	плинтус	плинтус МДФ, h 80 мм, аналог: плинтус МДФ под покраску 80×16	Farrow & Ball No. 2003 «Pointing»	2 м
О4	потолок	окраска, Tikkurila Euro Power 7, глубокоматовая, подготовка Q3	Tikkurila G503 «Calla»	12 м²

Примечания

1. Размеры — в мм от чистовых поверхностей стен; условные обозначения и общие указания — лист 4.

					Проект: Квартира 68 м², элитный модерн	М 1:20
	Лист	№ док.	Подпись	Дата		
Дизайнер	Кырлан А.С.			04.11.26	Развёртка стены Г. Кухня-столовая (пом. 5)	Стадия: П; Лист: 66; Листов: 86

выпуск 04.11.2026 № f0db2de63c · стр. 66 из 86

Развёртка стены А


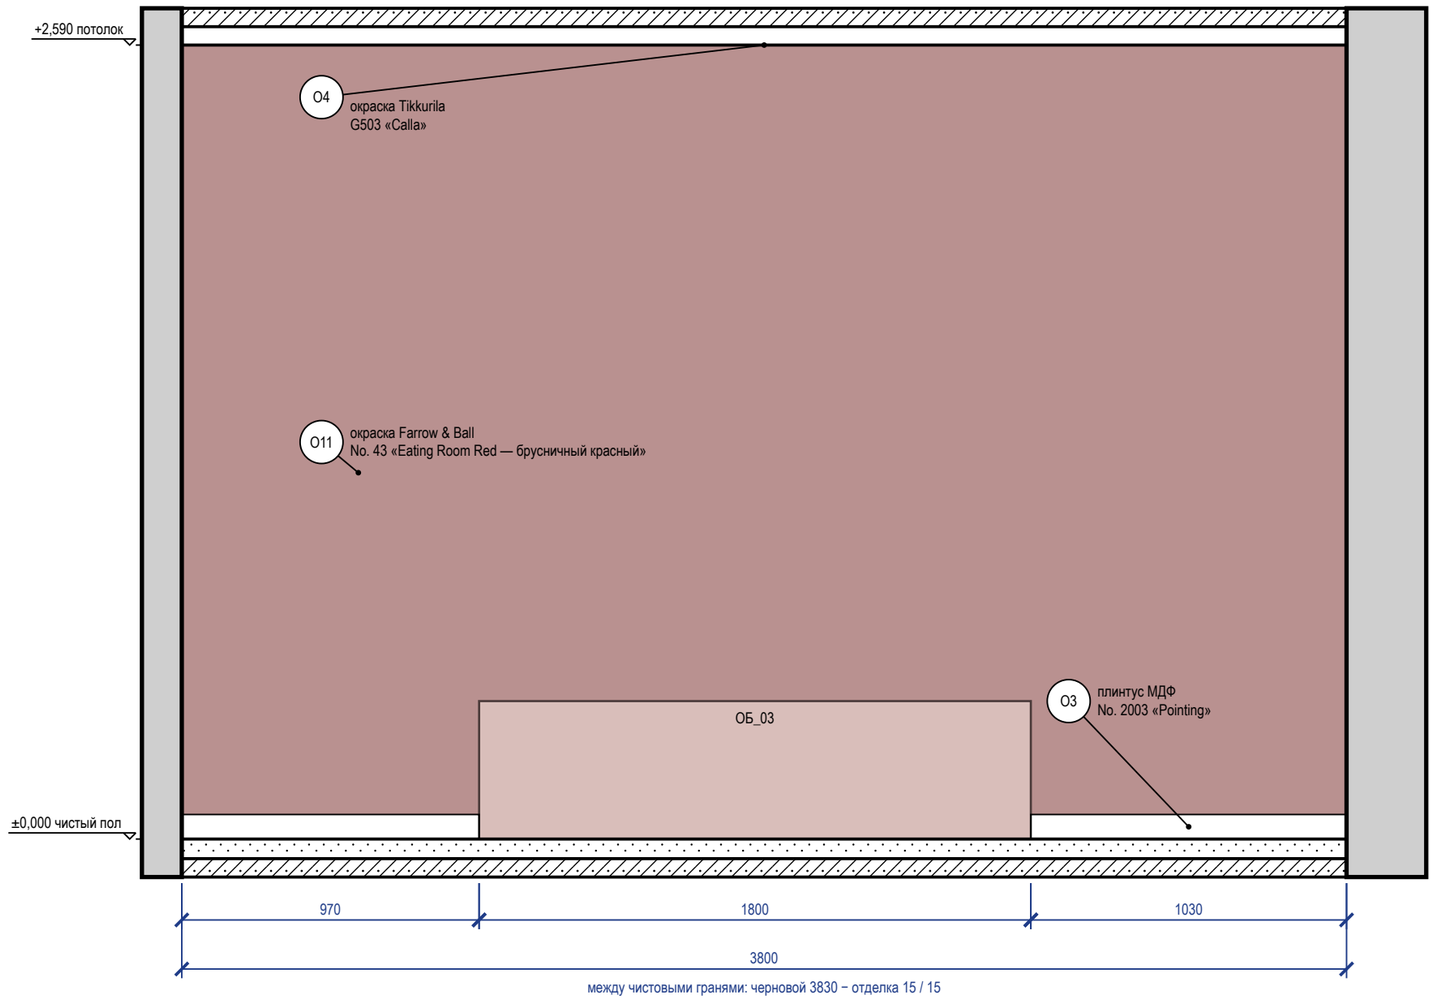


Схема развёрток (М 1:100)

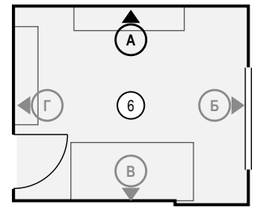

Ведомость отделки (на листе)

Марка	Поверхность	Материал, изделие	Цвет, код	Кол.
О3	плинтус	плинтус МДФ, h 80 мм, аналог: плинтус МДФ под покраску 80×16	Farrow & Ball No. 2003 «Pointing»	2 м
О4	потолок	окраска, Tikkurila Euro Power 7, глубокоматовая, подготовка Q3	Tikkurila G503 «Calla»	12,2 м²
О11	акцентная стена	окраска, Farrow & Ball Modern Emulsion, матовая, подготовка Q3	Farrow & Ball No. 43 «Eating Room Red — брусничный красный»	9,8 м²

Примечания

1. Размеры — в мм от чистовых поверхностей стен; условные обозначения и общие указания — лист 4.
2. Стена А показана двумя видами: здесь — архитектурная развёртка (мебель, отделка, проёмы, высоты), электроточки и выводы ВК с привязками и таблицей — на листе 68 («Привязки»).

					Проект: Квартира 68 м², элитный модерн	М 1:20
	Лист	№ док.	Подпись	Дата		
Дизайнер	Кырлан А.С.			04.11.26	Развёртка стены А. Гостиная (пом. 6)	Стадия: П; Лист: 67; Листов: 86

Правка к этому листу

Развёртка стены А: электроточки и выводы

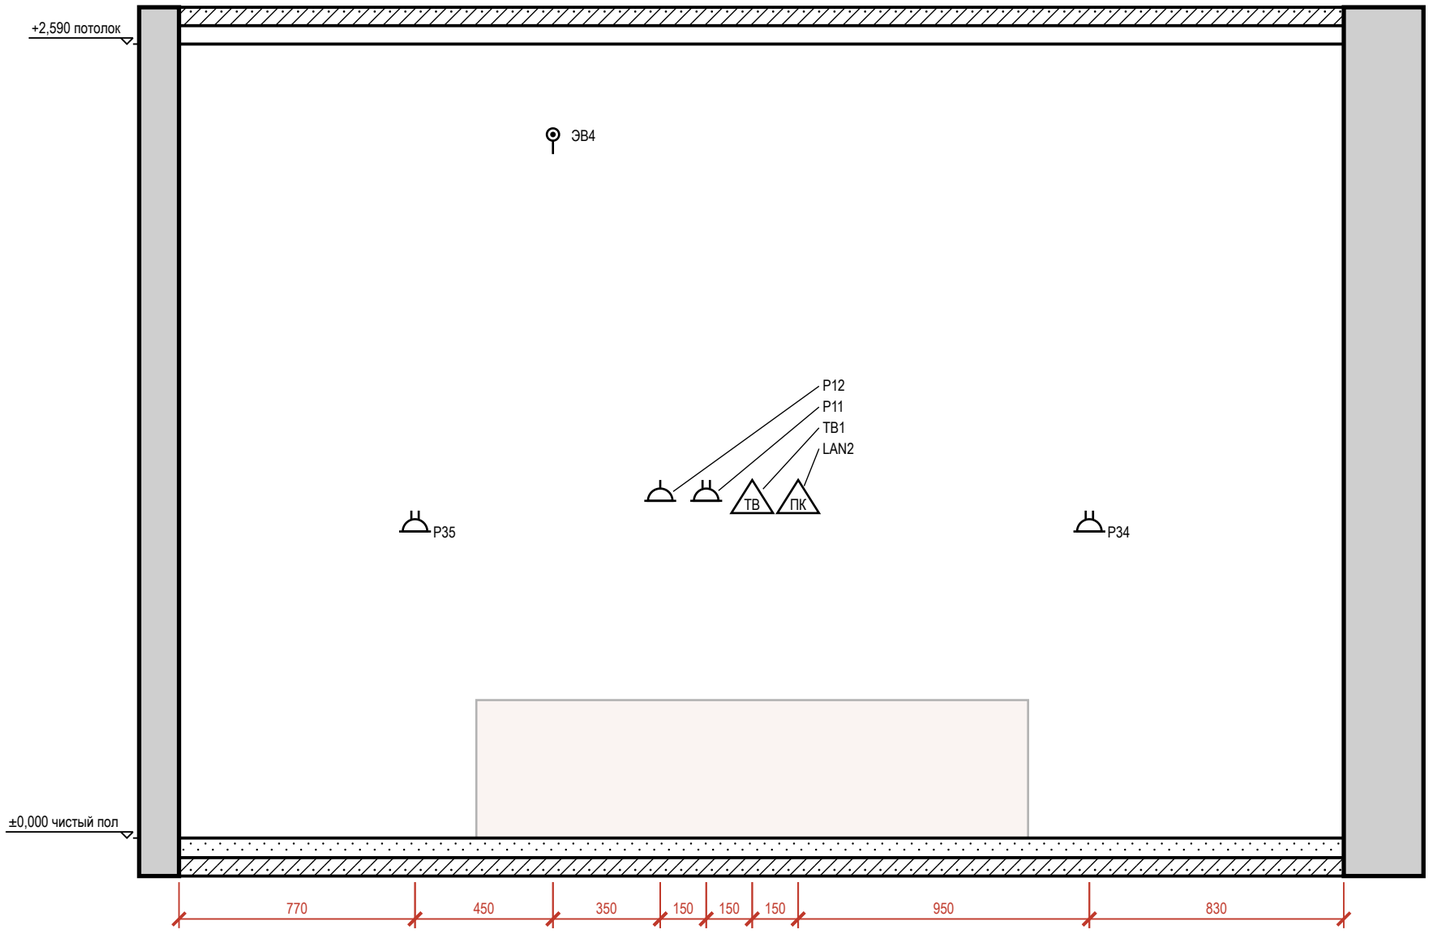



Таблица привязок электроточек и выводов

Марка	Назначение	От угла, мм	H от пола, мм	Примечание
P35	розетка: ТВ-зона: приставка, консоль, саундбар	770	1000	рамка 2 поста, гр. 5
ЭВ4	вывод кабеля: кондиционер КВ-1 — вывод питания внутреннего блока	1220	2295	гр. 17
P12	розетка: саундбар	1570	1100	гр. 5
P11	розетка: ТВ, приставка	1720	1100	рамка 2 поста, гр. 5
TB1	розетка ТВ: ТВ-зона	1870	1100	
LAN2	розетка RJ45: Smart TV	2020	1100	
P34	розетка: ТВ-зона: приставка, консоль, саундбар	2970	1000	рамка 2 поста, гр. 5

Условные обозначения

- розетка с заземляющим контактом; у знака — марка, ×N постов в рамке, гр. — группа щита, H — высота оси, мм
- вывод кабеля для подключения прибора (без розетки), марка ЭВ
- ПК — розетка компьютерная RJ45
- ТВ — розетка телевизионная
- привязки точек и выводов от угла и от пола, мм
- A — марка развёртки: буква стены, стрелка — взгляд

Схема развёрток (М 1:50)

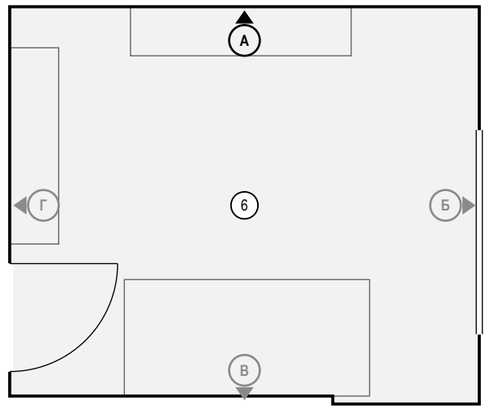

Примечания

1. Вид «Привязки» стены А — электроточки и выводы ВК; архитектурная развёртка (мебель, отделка, проёмы, высоты) — на листе 67. Мебель и приборы — подложкой для ориентира; их марки и обозначения мебели, проёмов и стен — там же.
2. Привязки — в мм: по горизонтали от левого чистового угла стены до оси изделия, H — от чистого пола до оси; все точки — в таблице привязок. Красная цепочка — привязки по осям; точки ближе 120 мм одна к другой в цепочку не дробятся — их привязки только в таблице.
3. У знака — марка электроточки (P — розетка, S — выключатель, Св — светильник, ЭВ — вывод кабеля); условные обозначения и общие указания — лист 4.

					Проект: Квартира 68 м², элитный модерн — М 1:20
	Лист	№ док.	Подпись	Дата	
Дизайнер	Кырлан А.С.			04.11.26	Привязки электроточек, стена А. Гостиная (пом. 6)

Стадия	Лист	Листов
П	68	86

Правка к этому листу

Развёртка стены Б


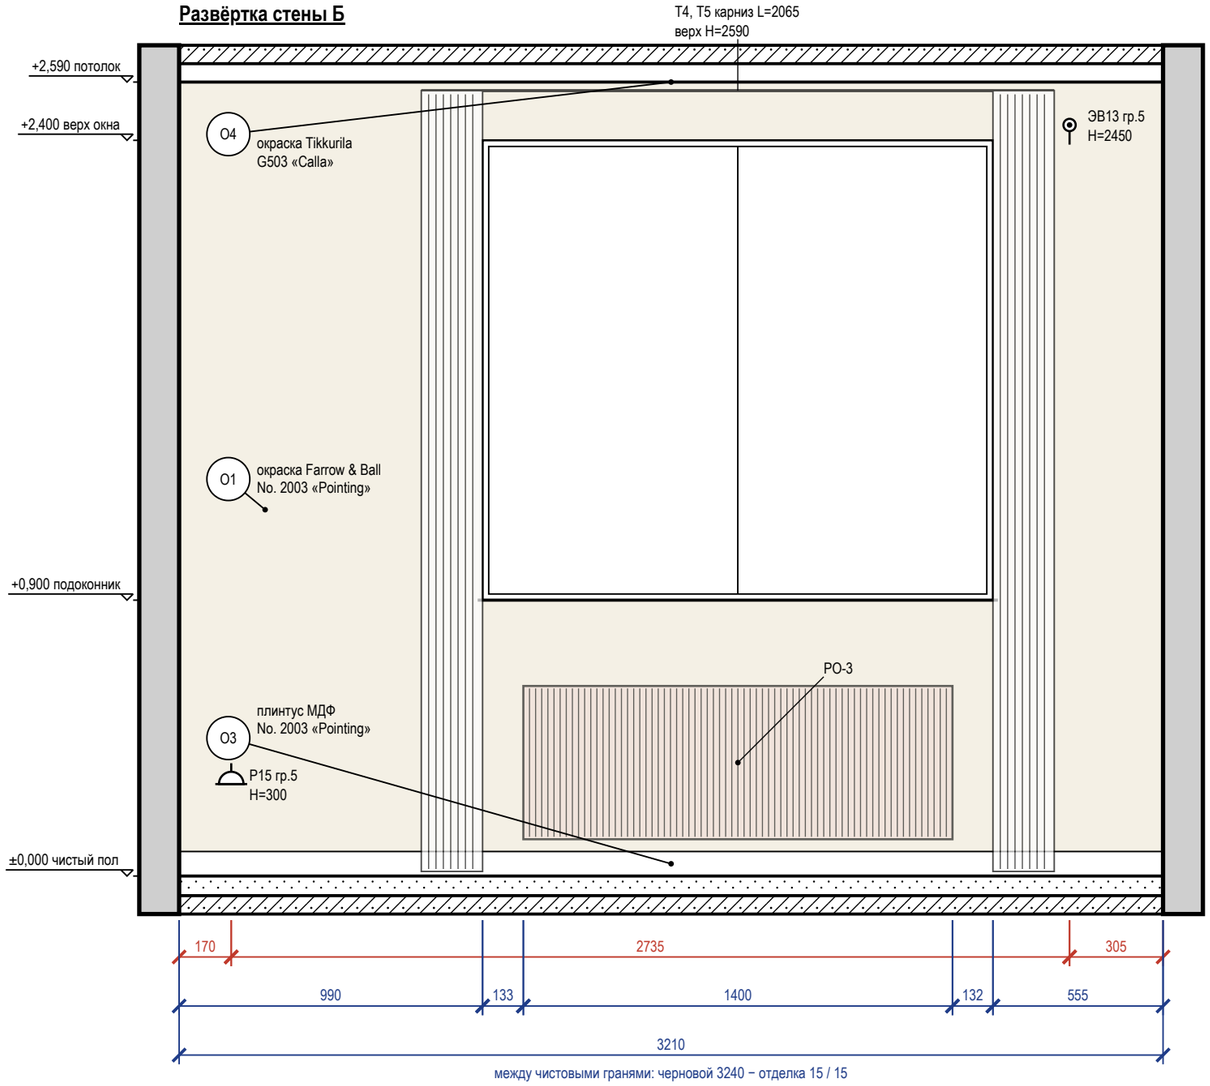


Схема развёрток (М 1:100)

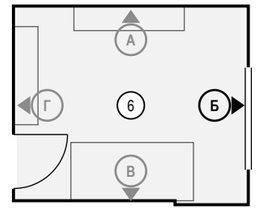

Ведомость отделки (на листе)

Марка	Поверхность	Материал, изделие	Цвет, код	Кол.
О1	стены	окраска, Farrow & Ball Modern Emulsion, матовая, подготовка Q3	Farrow & Ball No. 2003 «Pointing»	5,8 м²
О3	плинтус	плинтус МДФ, h 80 мм, аналог: плинтус МДФ под покраску 80×16	Farrow & Ball No. 2003 «Pointing»	3,2 м
О4	потолок	окраска, Tikkurila Euro Power 7, глубокоматовая, подготовка Q3	Tikkurila G503 «Calla»	12,2 м²

Примечания

1. Размеры — в мм от чистовых поверхностей стен; условные обозначения и общие указания — лист 4.
2. Карнизы (шины) — по ведомости текстиля декоратора: длина L и верх H на развёртке — те же числа, что в ведомости; крепление — до окраски потолка.

					Проект: Квартира 68 м², элитный модерн — М 1:20
	Лист	№ док.	Подпись	Дата	
Дизайнер	Кырлан А.С.			04.11.26	Развёртка стены Б. Гостиная (пом. 6)
					Стадия: П · Лист: 69 · Листов: 86

Правка к этому листу

Развёртка стены В


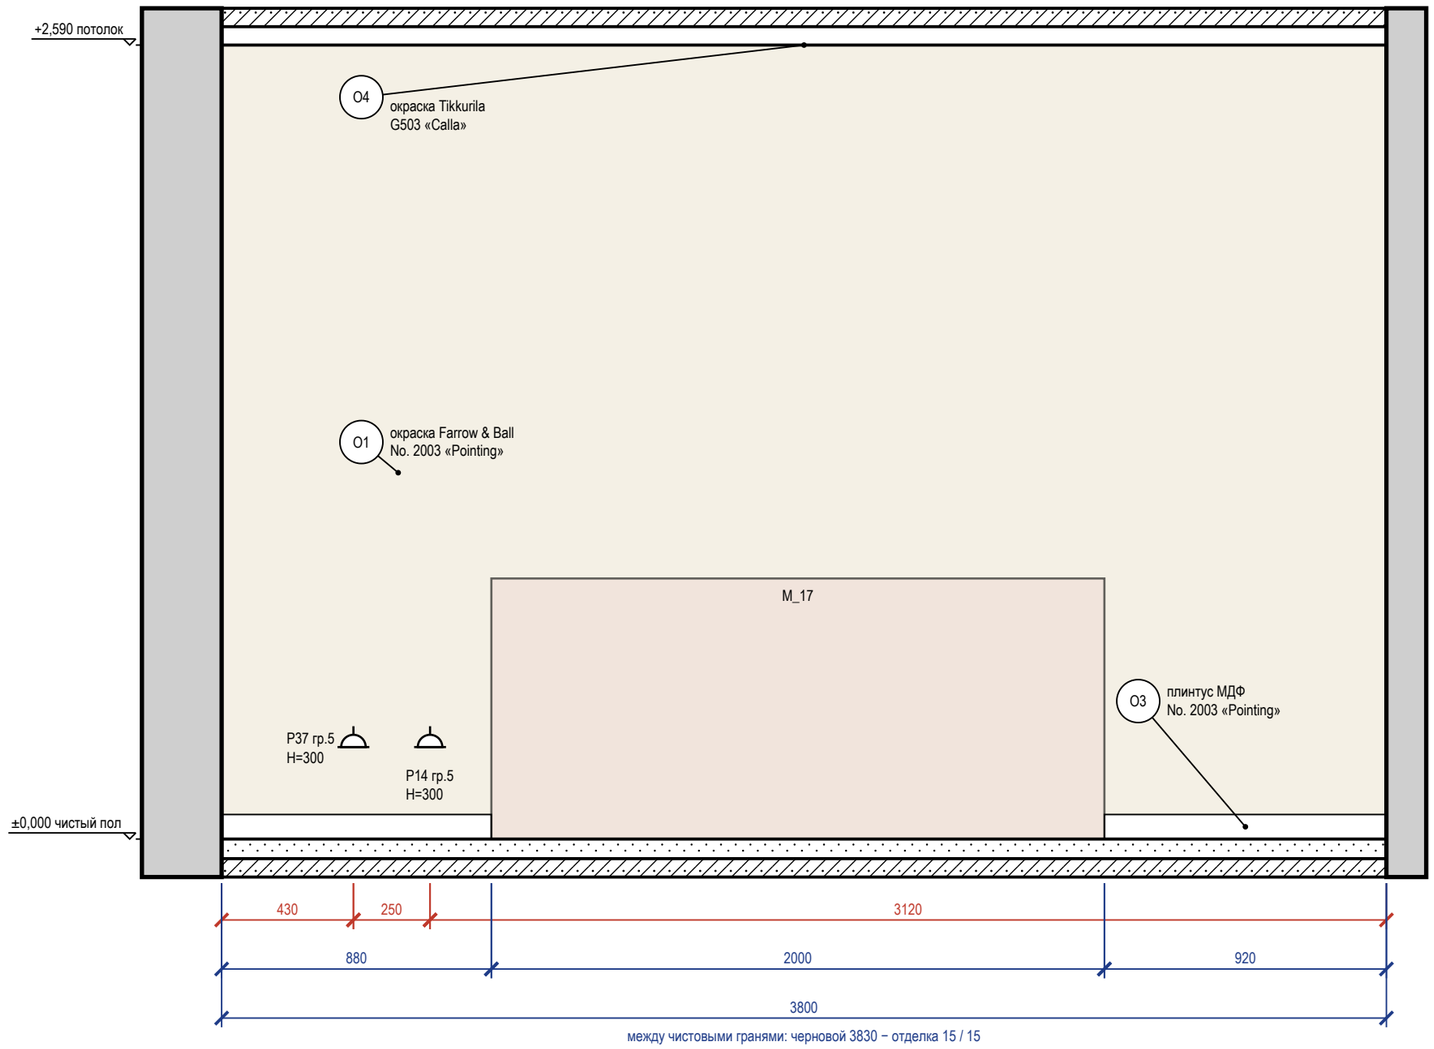


Схема развёрток (М 1:100)

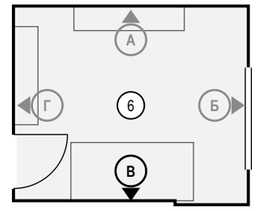


Ведомость отделки (на листе)

Марка	Поверхность	Материал, изделие	Цвет, код	Кол.
О1	стены	окраска, Farrow & Ball Modern Emulsion, матовая, подготовка Q3	Farrow & Ball No. 2003 «Pointing»	9,8 м²
О3	плинтус	плинтус МДФ, h 80 мм, аналог: плинтус МДФ под покраску 80×16	Farrow & Ball No. 2003 «Pointing»	1,8 м
О4	потолок	окраска, Tikkurila Euro Power 7, глубокоматовая, подготовка Q3	Tikkurila G503 «Calla»	12,2 м²

4 **Плинтус МДФ 80×16 мм у окрашенной стены по доске (ламинату) (М 1:10)**

Узел 4 — лист С6

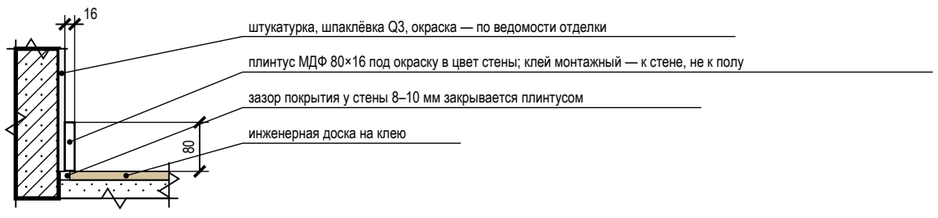

Примечания

1. Размеры — в мм от чистовых поверхностей стен; условные обозначения и общие указания — лист 4.

					Проект: Квартира 68 м², элитный модерн — М 1:20
	Лист	№ док.	Подпись	Дата	
Дизайнер	Кырлан А.С.			04.11.26	Развёртка стены В. Гостиная (пом. 6)
					Стадия: П; Лист: 70; Листов: 86

выпуск 04.11.2026 № f0db2de63c · стр. 70 из 86

Правка к этому листу

Развёртка стены Г


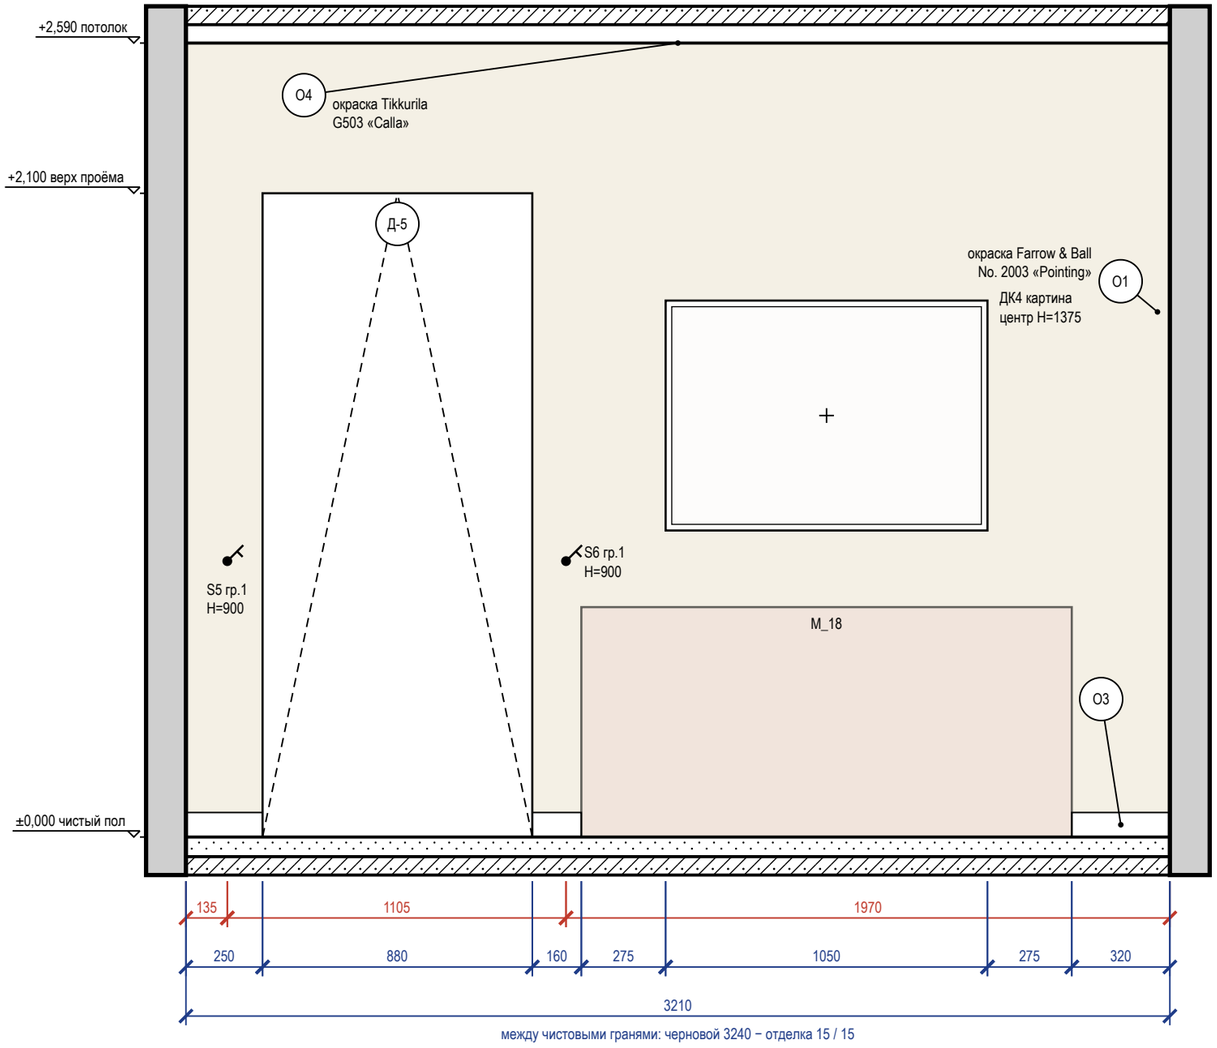


Схема развёрток (М 1:100)

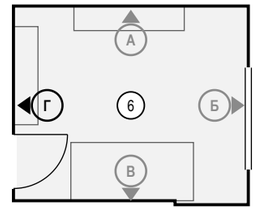

Ведомость отделки (на листе)

Марка	Поверхность	Материал, изделие	Цвет, код	Кол.
О1	стены	окраска, Farrow & Ball Modern Emulsion, матовая, подготовка Q3	Farrow & Ball No. 2003 «Pointing»	6,5 м²
О3	плинтус	плинтус МДФ, h 80 мм, аналог: плинтус МДФ под покраску 80×16	Farrow & Ball No. 2003 «Pointing»	0,7 м
О4	потолок	окраска, Tikkurila Euro Power 7, глубокоматовая, подготовка Q3	Tikkurila G503 «Calla»	12,2 м²


Примечания

1. Размеры — в мм от чистовых поверхностей стен; условные обозначения и общие указания — лист 4.
2. Картины и зеркала крепить к основанию по паспорту изделия (закладные и анкеры — в перечне скрытых работ); крест — ось центра предмета.

					Проект: Квартира 68 м², элитный модерн — **М 1:20**
	Лист	№ док.	Подпись	Дата	Развёртка стены Г. Гостиная (пом. 6)
Дизайнер	Кырлан А.С.			04.11.26	

Стадия	Лист	Листов
П	71	86

Развёртка стены А1

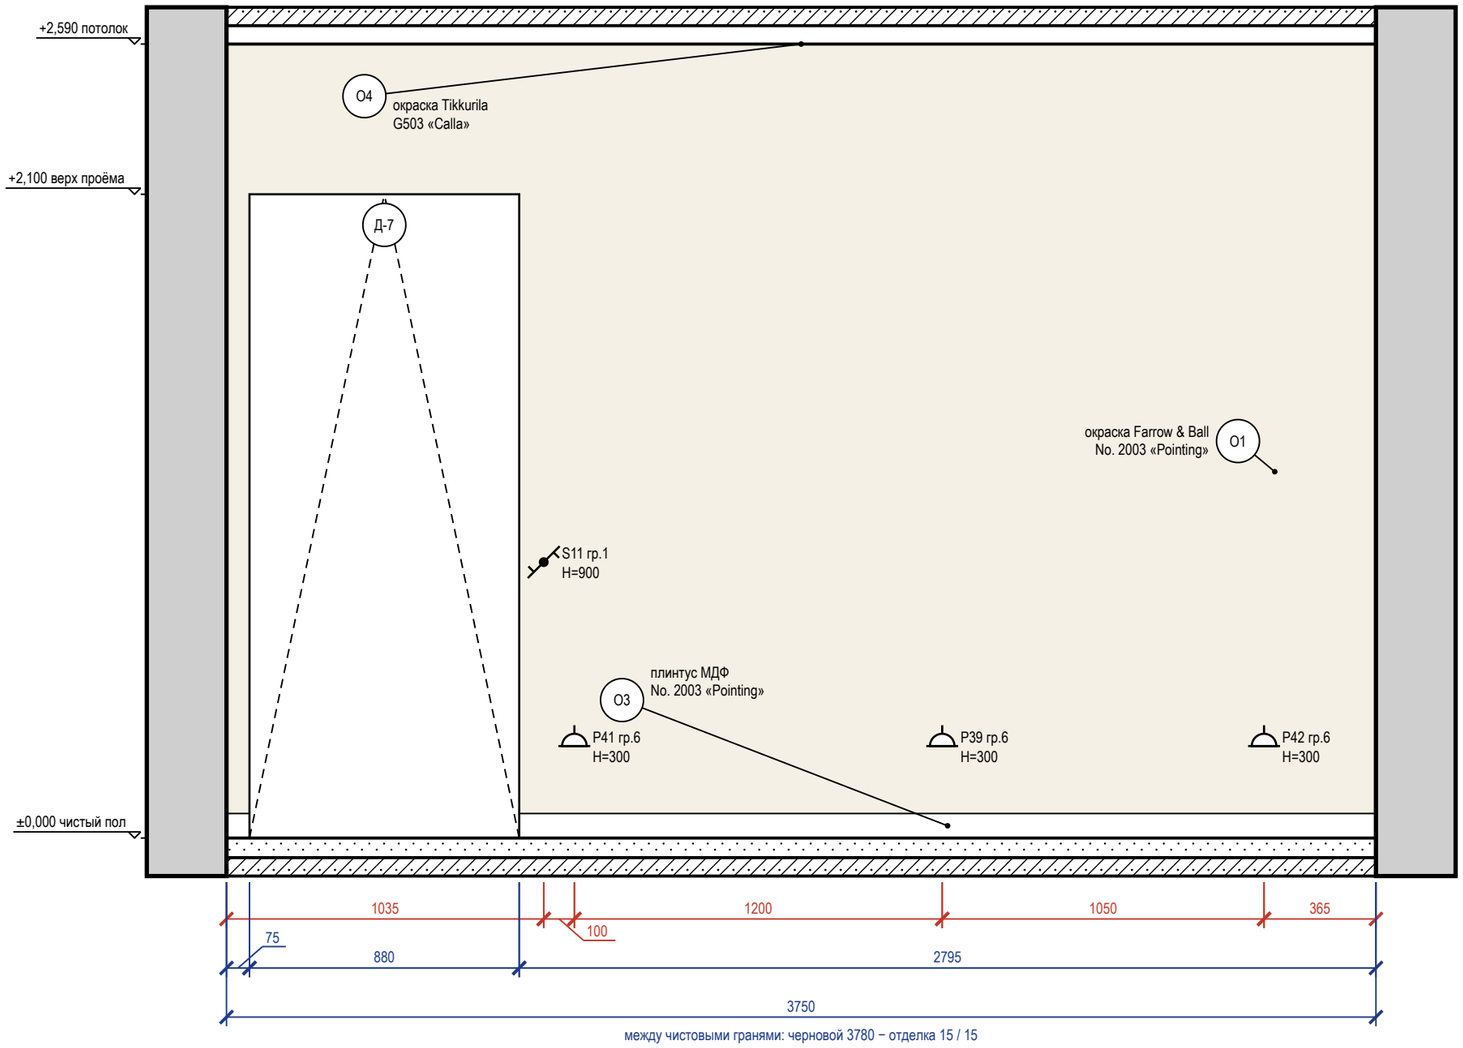

Развёртка стены А2


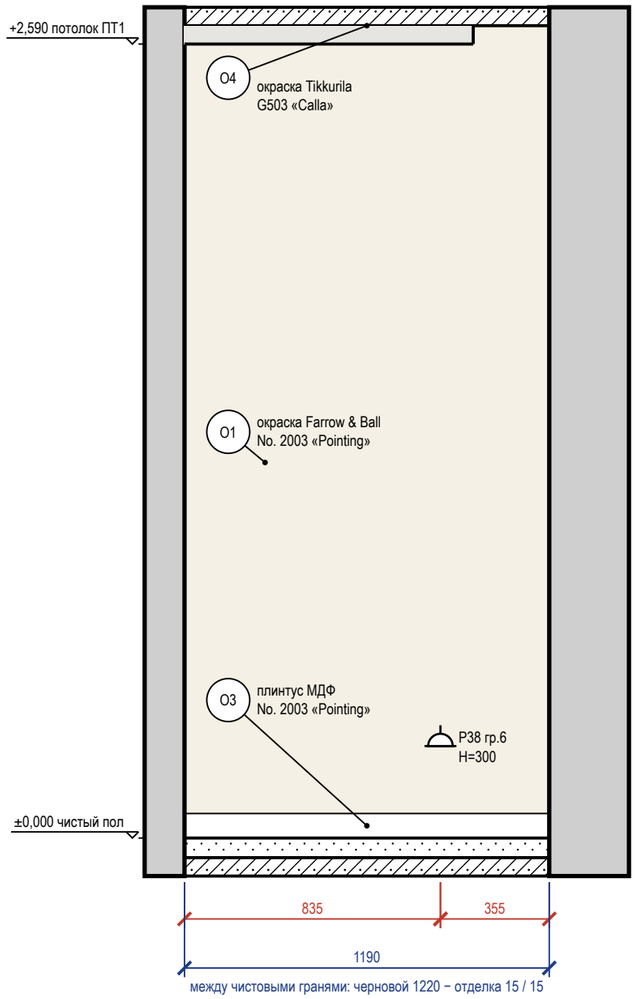


Схема развёрток (М 1:100)

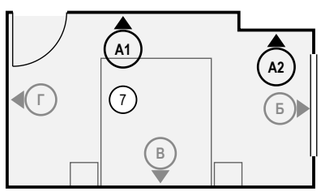

Ведомость отделки (на листе)

Марка	Поверхность	Материал, изделие	Цвет, код	Кол.
О1	стены	окраска, Farrow & Ball Modern Emulsion, матовая, подготовка Q3	Farrow & Ball No. 2003 «Pointing»	11 м²
О3	плинтус	плинтус МДФ, h 80 мм, аналог: плинтус МДФ под покраску 80×16	Farrow & Ball No. 2003 «Pointing»	4,1 м
О4	потолок	окраска, Tikkurila Euro Power 7, глубокоматовая, подготовка Q3	Tikkurila G503 «Calla»	13,9 м²

Примечания


1. Размеры — в мм от чистовых поверхностей стен; условные обозначения и общие указания — лист 4.

					Проект: Квартира 68 м², элитный модерн — М 1:20
	Лист	№ док.	Подпись	Дата	
Дизайнер	Кырлан А.С.			04.11.26	Развёртки стен А1, А2. Спальня (пом. 7)

Стадия	Лист	Листов
П	72	86

выпуск 04.11.2026 № f0db2de63c · стр. 72 из 86

Развёртка стены Б

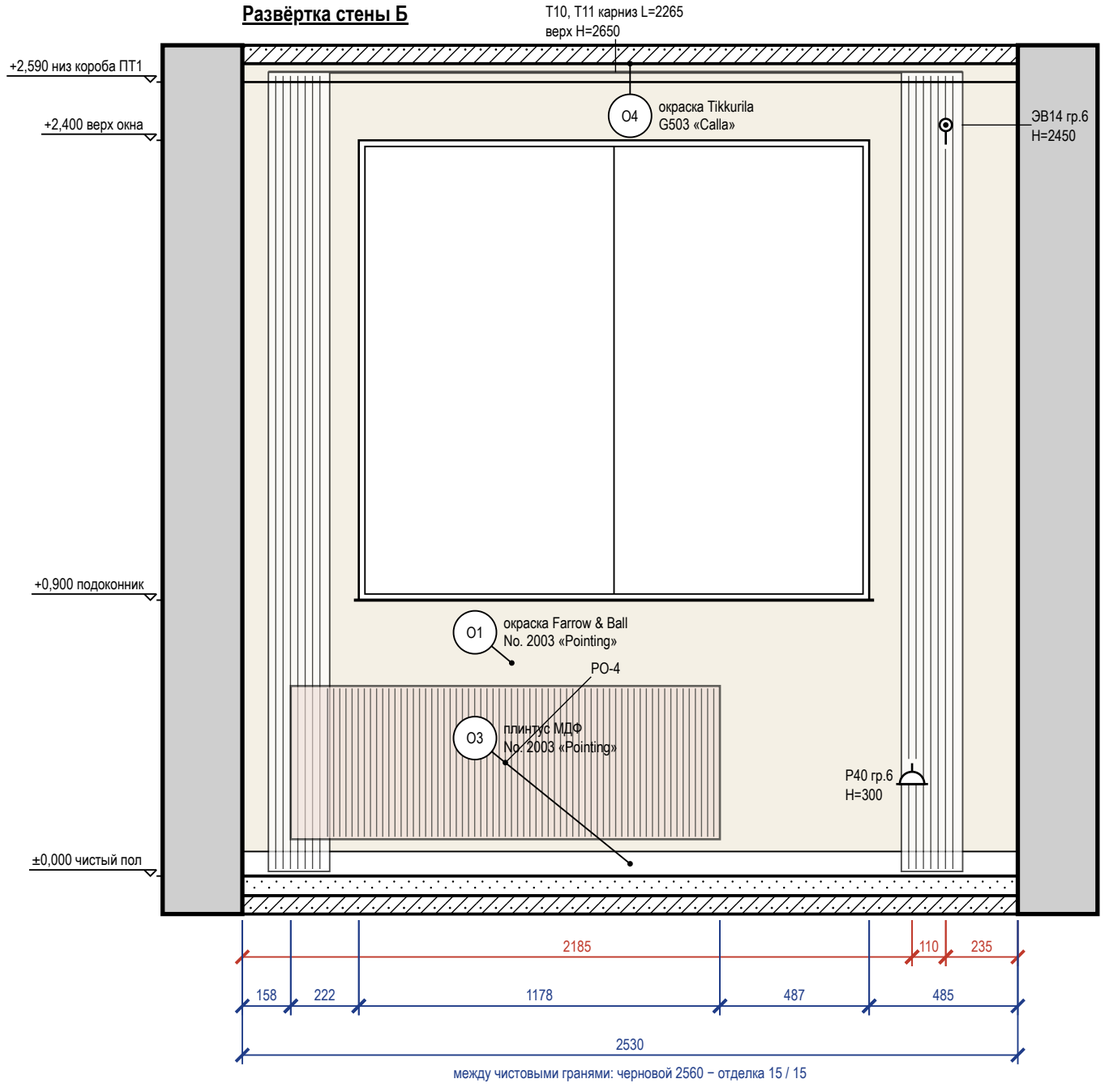

Развёртка стены Г


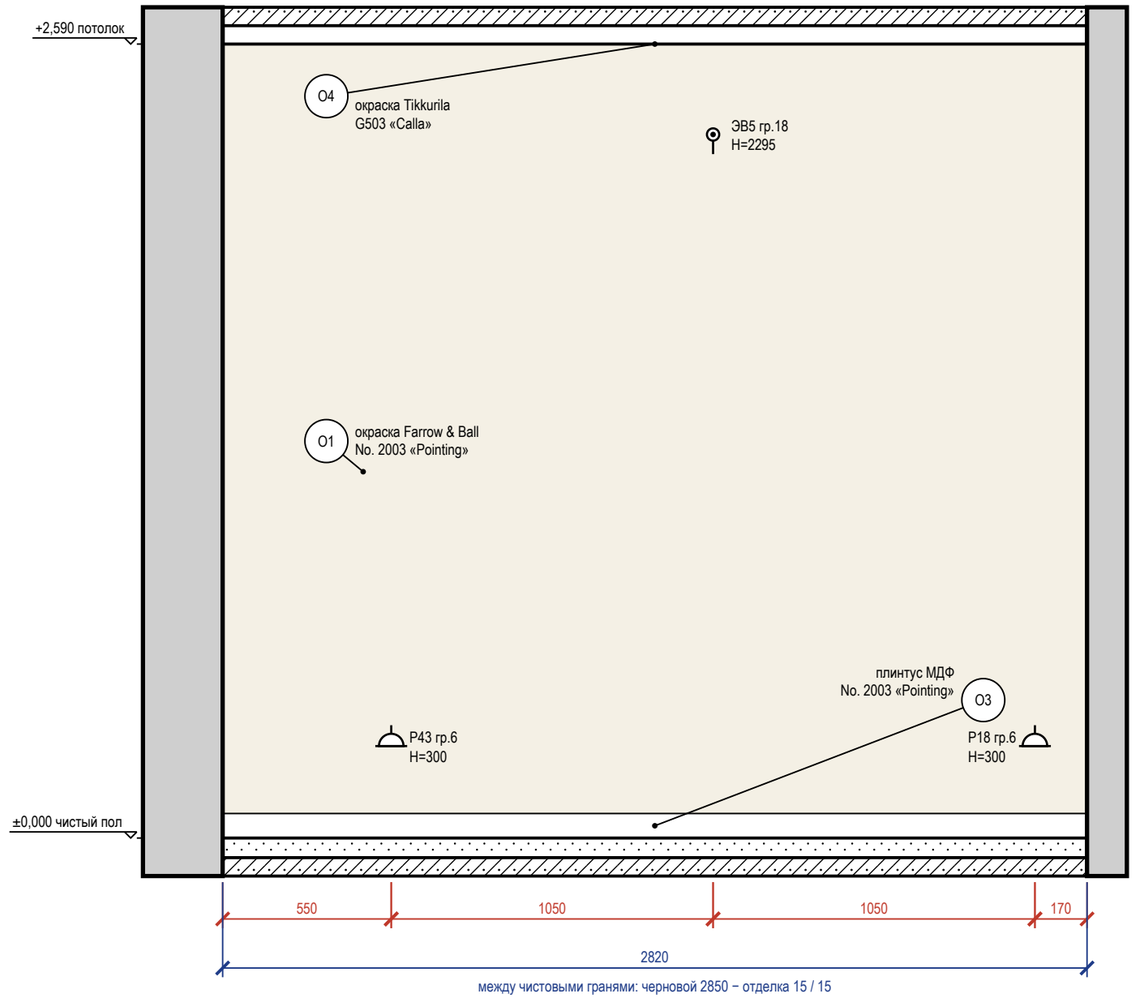


Схема развёрток (М 1:100)

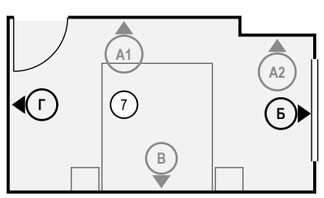

Ведомость отделки (на листе)

Марка	Поверхность	Материал, изделие	Цвет, код	Кол.
O1	стены	окраска, Farrow & Ball Modern Emulsion, матовая, подготовка Q3	Farrow & Ball No. 2003 «Pointing»	11,5 м²
O3	плинтус	плинтус МДФ, h 80 мм, аналог: плинтус МДФ под покраску 80×16	Farrow & Ball No. 2003 «Pointing»	5,3 м
O4	потолок	окраска, Tikkurila Euro Power 7, глубокоматовая, подготовка Q3	Tikkurila G503 «Calla»	13,9 м²

Примечания

1. Размеры — в мм от чистовых поверхностей стен; условные обозначения и общие указания — лист 4.
2. Карнизы (шины) — по ведомости текстиля декоратора: длина L и верх H на развёртке — те же числа, что в ведомости; крепление — до окраски потолка.
3. Линии узора (швы плитки, складки штор, рёбра радиаторов) прерываются у знаков и выносок — просвет между линиями не менее 0,7 мм.

					Проект: Квартира 68 м², элитный модерн	М 1:20
	Лист	№ док.	Подпись	Дата		
Дизайнер	Кырлан А.С.			04.11.26	Развёртки стен Б, Г. Спальня (пом. 7)	Стадия: П; Лист: 73; Листов: 86

Правка к этому листу

Развёртка стены В


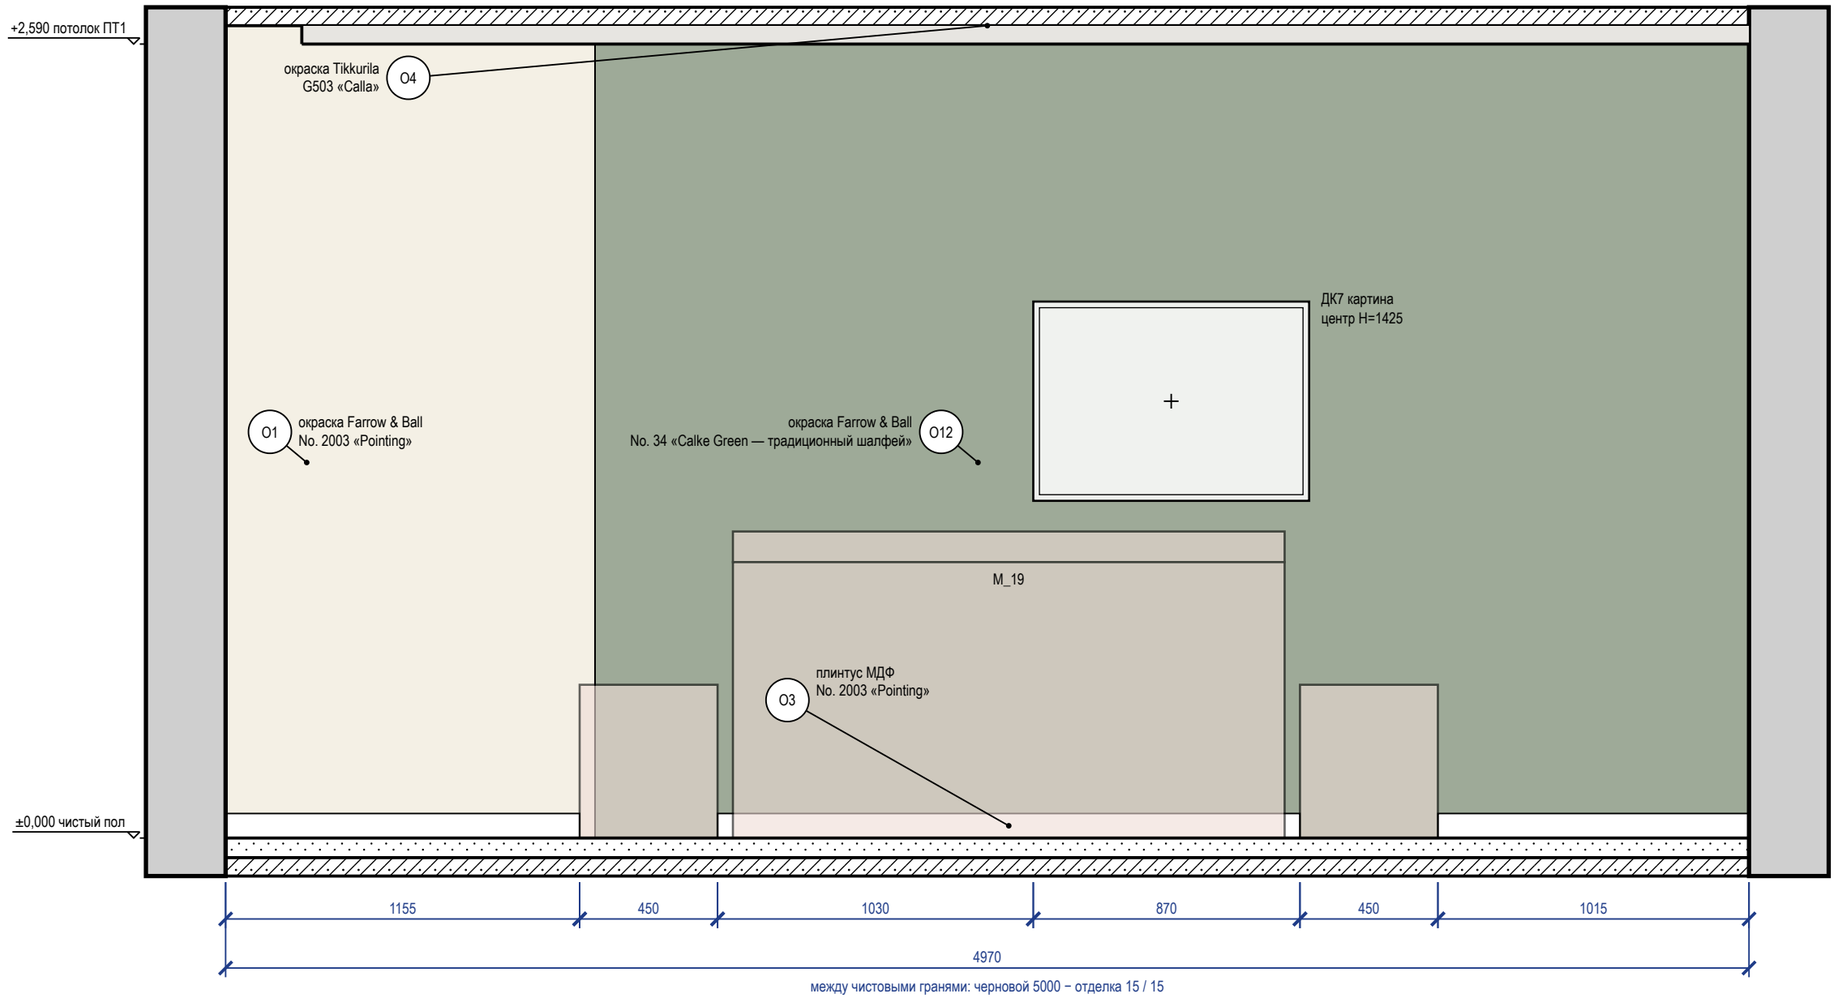


Схема развёрток (М 1:100)

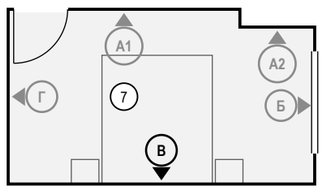

Ведомость отделки (на листе)

Марка	Поверхность	Материал, изделие	Цвет, код	Кол.
О1	стены	окраска, Farrow & Ball Modern Emulsion, матовая, подготовка Q3	Farrow & Ball No. 2003 «Pointing»	3,2 м²
О3	плинтус	плинтус МДФ, h 80 мм, аналог: плинтус МДФ под покраску 80×16	Farrow & Ball No. 2003 «Pointing»	4,1 м
О4	потолок	окраска, Tikkurila Euro Power 7, глубокоматовая, подготовка Q3	Tikkurila G503 «Calla»	13,9 м²
О12	акцентная стена	окраска, Farrow & Ball Modern Emulsion, матовая, подготовка Q3	Farrow & Ball No. 34 «Calke Green традиционный шалфей»	10 м²

Примечания

1. Размеры — в мм от чистовых поверхностей стен; условные обозначения и общие указания — лист 4.
2. Стена В показана двумя видами: здесь — архитектурная развёртка (мебель, отделка, проёмы, высоты), электроточки и выводы ВК с привязками и таблицей — на листе 75 («Привязки»).
3. Картины и зеркала крепить к основанию по паспорту изделия (закладные и анкеры — в перечне скрытых работ); крест — ось центра предмета.

					Проект: Квартира 68 м², элитный модерн	М 1:20
	Лист	№ док.	Подпись	Дата		
Дизайнер	Кырлан А.С.			04.11.26	Развёртка стены В. Спальня (пом. 7)	

Стадия	Лист	Листов
П	74	86

Развёртка стены В: электроточки и выводы

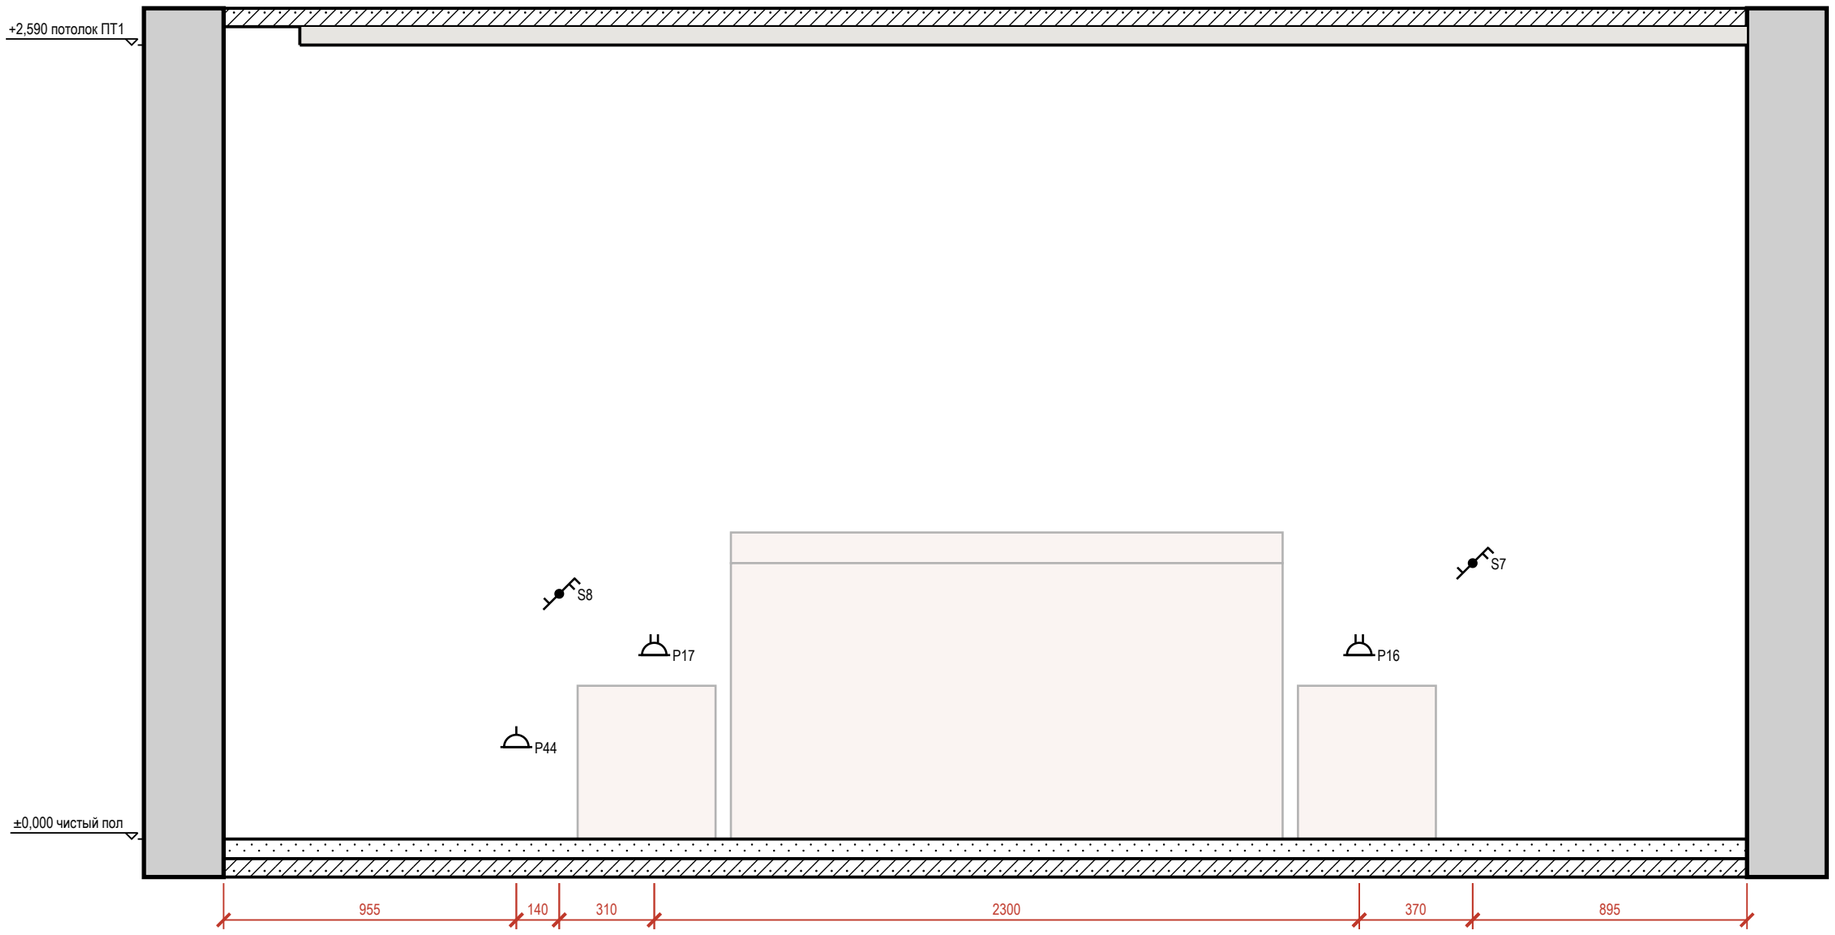



Таблица привязок электроточек и выводов

Марка	Назначение	От угла, мм	H от пола, мм	Примечание
P44	розетка: общего назначения	955	300	гр. 6
S8	выключатель	1095	800	гр. 1
P17	розетка: у кровати: лампа, зарядка	1405	600	рамка 2 поста, гр. 6
P16	розетка: у кровати: лампа, зарядка	3705	600	рамка 2 поста, гр. 6
S7	выключатель	4075	900	гр. 1

Условные обозначения

- розетка с заземляющим контактом; у знака — марка, ×N постов в рамке, гр. — группа щита, H — высота оси, мм
- выключатель одноклавишный
- выключатель двухклавишный (флажков — по числу клавиш)
- выключатель с проходной или перекрёстной клавишей (обратный флажок); тип клавиши — в подписи
- привязки точек и выводов от угла и от пола, мм
- (A) марка развёртки: буква стены, стрелка — взгляд

Схема развёрток (М 1:100)

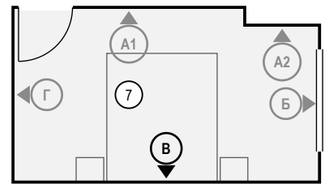

Примечания

1. Вид «Привязки» стены В — электроточки и выводы ВК; архитектурная развёртка (мебель, отделка, проёмы, высоты) — на листе 74. Мебель и приборы — подложкой для ориентира; их марки и обозначения мебели, проёмов и стен — там же.
2. Привязки — в мм: по горизонтали от левого чистового угла стены до оси изделия, H — от чистого пола до оси; все точки — в таблице привязок. Красная цепочка — привязки по осям; точки ближе 120 мм одна к другой в цепочку не дробятся — их привязки только в таблице.
3. У знака — марка электроточки (P — розетка, S — выключатель, Св — светильник, ЭВ — вывод кабеля); условные обозначения и общие указания — лист 4.

					Проект: Квартира 68 м², элитный модерн	М 1:20
	Лист	№ док.	Подпись	Дата	Привязки электроточек, стена В. Спальня (пом. 7)	Стадия / Лист / Листов
Дизайнер	Кырлан А.С.			04.11.26		П / 75 / 86

Комплект предварительный по пунктам этих таблиц. Пока по пункту нет ответа или решения, показанное на указанном листе — допущение проектировщика, а не утверждённое решение.
Сводка: открытых вопросов — 25 (из них ждут факта объекта — 7: контрольного обмера, обследования или документа); изменений в реестре — 7.

Открытые вопросы и принятые допущения

№	Формулировка	Вид	Кто решает	Если решения нет	Лист, где это проявляется
К-1	Планировка принята по обводу плана заказчика, без обмера: план заказчика распознан автоматически по картинке (1 модель ИИ, масштаб — размерные цепочки), затем исправлен исполнителем вручную по размерным числам и рисунку плана (15 правок) и не проверен дизайнером: положение помещений, стен и проёмов — по обводу, контрольный обмер на объекте не выполнялся. От этого зависят все размеры альбома, площади, заказ материалов и изделий. Нужны план БТИ / проект дома и контрольный обмер; до них планировочное решение заменяется обводом плана и уточняется обмером.	Непонятно Ждёт: документа, обмера	Архитектор-планировщик	размеры и расстановка на листах — предложение проектировщика по брифу; мебель на заказ, двери и материалы по ним не заказывать	л. 6 — План планировки (подобрана проектировщиком, плана заказчика нет) л. 29 — План размещения дверей л. 12 — План размещения мебели и оборудования
К-3	Тип дома, конструкция перекрытия и несущие стены в брифе не указаны; проект дома, план БТИ и техническое заключение не переданы. До их получения все существующие стены считаются несущими.	Отсутствует Ждёт: документа	Архитектор-планировщик	все существующие стены считаются несущими; демонтаж и штробление в них не выполняются до технического заключения	л. 6 — План планировки (подобрана проектировщиком, плана заказчика нет) полный альбом
К-4	Стояки: на плане потолков есть только знак ∅ в верхнем левом углу ванной (120 мм от стены) — принят за стояк канализации К1 Ø110; стояки В1 и Т3 на плане не показаны и приняты в том же коробе (предложение). Варианты значения знака: стояк / вентканал / вытяжка. Нужен план с инженерией или обмер; от стояков зависят трассы, уклоны и выпуски.	Непонятно Ждёт: обмера	Инженер ВК (вода, канализация)	стояки К1, В1, Т3 в коробе в углу ванной; трассы и уклоны — от них, к монтажу после обмера	л. 17 — План выводов сантехники л. 18 — Схема разводки водопровода и канализации
К-5	Вентканалы в брифе не показаны: приняты у санузла и кухни. От них зависят вытяжка санузла, вытяжка над плитой (до обмера рециркуляция) и короба потолка.	Отсутствует Ждёт: обмера	Инженер ОВ	вытяжка кухни — рециркуляционная; вентилятор санузла по месту канала после обмера	л. 41 — План вентиляции л. 17 — План выводов сантехники
К-6	Разрешённая мощность по ТУ в брифе не указана; принята 10 кВт (квартира с электроплитой). Тип плиты и система заземления в брифе тоже не указаны: приняты электрическая варочная панель и TN-C-S (PE-проводник от ввода) — от них зависят группа плиты, вводной аппарат и защитное заземление. Передать ТУ или справку УК (мощность, система заземления, наличие газа).	Отсутствует Ждёт: документа	Инженер-электрик	щит и группы рассчитаны на 10 кВт, электроплита, TN-C-S; при других ТУ — пересчёт групп варочной панели и духового шкафа, при газе — задание газовику, при TN-C проект заземления	л. 34 — Однолинейная схема щита
К-7	Стиль выбран заказчиком в брифе: Современный (модерн); второй стиль quiet-luxury 40 % — предложение исполнителя (исполнитель, приём заказа 03.11.2026: в рассказе «элитный проект… премиальные материалы» — премиальная составляющая стиля: натуральный камень, широкая доска, шпон, глубокоматовые тёплые нейтрали), не выбор заказчика. Коды палитры подобраны исполнителем по веерам стиля (Современный (контемпорари) + Тихая роскошь (quiet luxury)): стены FarrowBall No. 2003, потолки Tikkurila G503, акценты по комнатам — NCS S 7010-Y50R, NCS S 6020-G70Y, FarrowBall No. 298. Выкрасы не делались. Утвердить стиль и коды по выкрасам.	Спорно Ждёт: решения	Колорист-комплектатор	коды — предложение исполнителя; краску, ткани и фасады не закупать до выкрасов	л. 11 — Колерная карта л. 12 — План размещения мебели и оборудования
К-8	Кухня, шкафы и встроенная техника описаны характеристиками («аналог по характеристикам»): модели не выбраны, ниши под технику — по паспорту выбранной модели. Выбрать технику и утвердить проект кухни.	Спорно Ждёт: решения	Мебельщик	выводы кухонной техники — после утверждения проекта кухни; мебель на заказ не заказывать	полный альбом л. 36 — План розеток и электровыводов
К-9	Состав семьи в брифе не указан (answers.household пуст): принято 2 человека. От числа жильцов зависят обеденная группа, хранение, нагрузка на санузлы и расчётная мощность. Уточнить у заказчика.	Отсутствует Ждёт: решения	Дизайнер интерьера	расстановка и расчёты — на 2 человека	л. 12 — План размещения мебели и оборудования л. 34 — Однолинейная схема щита
К-10	Заказчик указал в брифе, что плана нет и нужен обмер: все размеры альбома до обмера — допущение.	Отсутствует Ждёт: обмера	Архитектор-планировщик	альбом не выдаётся к работам до обмера	л. 6 — План планировки (подобрана проектировщиком, плана заказчика нет)
К-14	Эркер кухни обмерен частично: окно 1300 мм, глубина ≈ 570 мм, скос к нижней стене ≈ 45° (на листе не обмерен, по рисунку ≈ 1150 мм, вероятно, тоже остеклён). В альбоме эркер приведён к прямоугольнику ступенькой (площадь сохранена ±0,15 м²), окно на скосе не показано. Нужен обмер эркера: длины граней, углы, окна.	Непонятно Ждёт: решения	Архитектор-планировщик	эркер — ступенькой, окно только на прямой грани; ниша штор по эркеру — по плану потолков (250 мм)	л. 6 — План планировки (подобрана проектировщиком, плана заказчика нет)
К-15	В верхней (наружной?) стене кухни на плане два узких разрыва ≈ 130 мм (над лентой 13) с участком стены 650 мм между ними. Это вентканалы, окно или проходы коммуникаций — по плану потолков не понять. В альбоме не показаны.	Непонятно Ждёт: решения	Архитектор-планировщик	не учитываются; кухонный гарнитур вдоль верхней стены до проверки на месте	л. 6 — План планировки (подобрана проектировщиком, плана заказчика нет)
К-16	Входная дверь на плане не помечена (марки Д-1…Д-5 — межкомнатные). Принят вход через проём 880 мм в нижней стене прихожей (единственный разрыв наружной стены без окна).	Непонятно Ждёт: решения	Архитектор-планировщик	вход — там; входной блок — по замеру проёма	л. 6 — План планировки (подобрана проектировщиком, плана заказчика нет)
К-17	Проём из прихожей в спальню (880 мм) без марки Д — это проём без двери или дверь, не попавшая в ведомость Д? Варианты: (1) дверь 800 с полотном, как остальные; (2) открытый проём. Рекомендация — (1): спальня не проходная.	Непонятно Ждёт: решения	Архитектор-планировщик	дверь 800 × 2100 с полотном, открывание в спальню	л. 6 — План планировки (подобрана проектировщиком, плана заказчика нет)
К-18	В правом верхнем углу спальни прямоугольник ≈ 1300 × 290 мм вне контура потолка (без подписи): короб, шахта, пилон или шкаф. В альбоме — вне помещения.	Непонятно Ждёт: решения	Архитектор-планировщик	участок вне помещения, мебель к нему не ставится	л. 6 — План планировки (подобрана проектировщиком, плана заказчика нет)
К-19	У левой стены кухни рядом с Д-4 на плане синий участок «залізобетон» ≈ 640 × 90 мм (выступ стены, ригель или колонна?). В альбоме не показан.	Непонятно Ждёт: решения	Архитектор-планировщик	не учитывается до обмера	л. 6 — План планировки (подобрана проектировщиком, плана заказчика нет)

					Проект: Квартира 68 м², элитный модерн		
	Лист	№ док.	Подпись	Дата	Открытые вопросы, принятые допущения и конфликты. Лист 1 из 3	Стадия	Лист	Листов
Дизайнер	Кырлан А.С.			04.11.26		П	76	86

Открытые вопросы и принятые допущения (продолжение)

№	Формулировка	Вид	Кто решает	Если решения нет	Лист, где это проявляется
К-20	Светильники перенесены с исходного плана: марки 01-А, 01-Б, 02, 03, 04, 05, 06-А, 06-Б, 08-А, 08-Б, 09, 10, 12 (бра), 13 (подсветка рабочей поверхности), 13-А, 13-Б, 14 и вентиляторы 11 — место по плану (±30 мм по рисунку), но ведомости светильников нет: тип, мощность, световой поток, цвет света не заданы. Приняты: точечные LED 7 Вт 3000 K Ra ≥ 90; 13-А/13-Б — подвесные у кровати; 12 — настенное бра h 1200 (высота не задана); 09 в чёрной нише — трековые/точечные. Марка 13 на плане двойная: «13 підсвітка роб. пов.» в кухне и «13-А/13-Б» в спальне. Нужны ведомость светильников и схема включения (группы А/Б?).	Непонятно Ждёт: решения	Инженер-электрик	светильники по марке плана с параметрами-допущениями; закупать только после ведомости	л. 38 — План освещения
К-21	Ниша в прихожей «покрасить в чорний (темно-сірий)» — кода цвета нет. Предложение: RAL 7016 (антрацит, из палитры стиля), глубокоматовая. Варианты: RAL 9005 (чёрный) / RAL 7016 / NCS S 8500-N. Потолки по плану — RAL 9010.	Непонятно Ждёт: решения	Колорист-комплектатор	RAL 7016 глубокоматовая; выкрас до покраски	л. 11 — Колерная карта
К-22	Сверка с ведомостью отделки потолка заказчика: по альбому ГКЛ 61,14 м² (в ведомости 60,14), ГКЛ влагостойкий 5,81 (3,83 санузел + ванная по размерам больше), шпаклёвка по ж/б 1,52 (4,08 — ниши по размерам меньше), всего 68,47 (68,05). Возможно, в ведомости санузел или его часть посчитан «по ж/б», а ниша штор эркера — со скосом. Какая ведомость верна — по обмеру; ведомость заказчика не подгоняется.	Спорно Ждёт: решения	Гипсокартонщик	объёмы — по чертежу альбома; перед закупкой — по обмеру	л. 30 — План потолков
К-23	Бюджет в брифе не указан («элитный проект, премиальные материалы» — уровень, не сумма). Смета посчитана по премиальным позициям стиля без потолка суммы.	Отсутствует Ждёт: решения	Сметчик	материалы премиум-уровня стиля; сумма — для согласования, не обязательство	полный альбом
К-24	Расчётная нагрузка 10,8 кВт (по коэффициентам спроса, без подгонки) больше принятой разрешённой 10 кВт (К-6; ТУ не переданы). Предложение: запросить у сетевой организации / УК увеличение выделенной мощности до 15 кВт — иначе электроплита, тёплый пол и кондиционеры одновременно не работают; либо снять часть нагрузки (тёплый пол, кондиционеры — они предложены по умолчанию).	Спорно Ждёт: решения	Инженер-электрик	щит собран на 10 кВт, расчётная выше разрешённой; тёплый пол и кондиционеры — предложения, к монтажу не принимать до ответа по мощности	л. 34 — Однолинейная схема щита
К-25	Узел ввода воды принят по умолчанию (предложение): на ХВС и ГВС — кран → фильтр грубой очистки → счётчик → обратный клапан → редуктор давления → кран с электроприводом (защита от протечек) → коллектор на 13 выходов; разводка — коллекторная, в стяжке пола, отдельной трубой к каждому прибору, без соединений в полу. Не известны: место узла и коллектора, давление на вводе, Ду вводов, наличие счётчиков и разрешённый способ учёта (УК) — положение стояков принято без обмера (К-4). Нужны обмер, справка УК и решение по составу узла.	Отсутствует Ждёт: решения	Инженер ВК (вода, канализация)	узел ввода, коллектор и электрокраны — предложение, место на листах условное; трубы и арматуру не закупать, штробы и закладные в стяжке не делать до обмера и решения	л. 18 — Схема разводки водопровода и канализации л. 17 — План выводов сантехники
К-26	Климатический подрайон (СП 131.13330) не задан: принят не северный — жилые комнаты и кухня под потолком от 2,5 м (СП 54, п. 5.12); в IA, IБ, IГ, IД, IVA — от 2,7 м.	Отсутствует Ждёт: документа	Архитектор-планировщик	отметки потолков жилых — по 2,5 м; при северном подрайоне уровни ниже 2,7 м пересчитать до заказа каркаса	л. 30 — План потолков
К-27	Унитаз подвесной C_01 (пом. 2 «Санузел»), выпуск К1-1 Ø110: выпуск Ø110 на высоте 220 мм в инсталляции; трасса до Ст К1-1 задана «в полу», а в пол она не помещается (нужно 210 мм при пироге 90 мм). Рекомендация исполнителя — короб 170×140 над чистым полом вдоль стен до Ст К1-1 (1,26 м): плитка обходит короб, у двери короб не проходит; это штатная прокладка для подвесного прибора: отвод идёт за инсталляцией и в коробе, пол не поднимается. Варианты: (а) короб 170×140 над чистым полом вдоль стен до Ст К1-1 (1,26 м): плитка обходит короб, у двери короб не проходит; (б) подиум или подъём пола на 120 мм — ступень и порог у входа, высота двери в свету и выводов прибора меняются, пересчёт раскладки плитки; (в) прибор ближе к стояку Ст К1-1 — меняется планировка санузла (расстановка, выводы, раскладка); (г) насосная установка (КНС) у прибора — шум, обслуживание, электропитание, согласование; только если другие варианты невозможны. Решение меняет санузел (высоты, раскладку плитки) — за автором с заказчиком.	Спорно Ждёт: решения	Инженер ВК (вода, канализация)	выпуск К1-1 и прибор C_01 не выполнять до решения; остальное — по листам	л. 18 — Схема разводки водопровода и канализации л. 17 — План выводов сантехники
К-28	Ванна C_04 (пом. 3 «Ванная»), выпуск К1-3 Ø50: в полу не помещается: врезка + перепад 62 (2,06 м × 30 мм/м) + Ø50 + слой над трубой 45 = 187 мм при пироге 90 мм. Рекомендация исполнителя — короб 150×110 над чистым полом вдоль стен до Ст К1-1 (2,06 м): плитка обходит короб, у двери короб не проходит; сифон и выпуск прибора — над полом за экраном/корпусом. Варианты: (а) короб 150×110 над чистым полом вдоль стен до Ст К1-1 (2,06 м): плитка обходит короб, у двери короб не проходит; (б) подиум или подъём пола на 100 мм — ступень и порог у входа, высота двери в свету и выводов прибора меняются, пересчёт раскладки плитки; (в) прибор ближе к стояку Ст К1-1 — меняется планировка санузла (расстановка, выводы, раскладка); (г) насосная установка (КНС) у прибора — шум, обслуживание, электропитание, согласование; только если другие варианты невозможны. Решение меняет санузел (высоты, раскладку плитки) — за автором с заказчиком.	Спорно Ждёт: решения	Инженер ВК (вода, канализация)	выпуск К1-3 и прибор C_04 не выполнять до решения; остальное — по листам	л. 18 — Схема разводки водопровода и канализации л. 17 — План выводов сантехники
К-29	Циркуляция ГВС в данных не задана — циркуляционного трубопровода на схеме нет. Решить: нужна ли циркуляция	Отсутствует Ждёт: решения	Инженер ВК (вода, канализация)	циркуляции на схеме нет	л. 22–25 — Развёртки мокрых зон: выводы ВК. Санузел л. 19 — Аксонометрическая схема В1 (холодное водоснабжение) л. 18 — Схема разводки водопровода и канализации

					Проект: Квартира 68 м², элитный модерн
	Лист	№ док.	Подпись	Дата	Открытые вопросы, принятые допущения и конфликты. Лист 2 из 3
Дизайнер	Кырлан А.С.			04.11.26	

Стадия	Лист	Листов
П	77	86

Изменения проекта после выпуска листов (реестр изменений)

№	Дата	Лист	Было	Стало	Кто решил, подпись
ИЗ-1	03.11.2026	л. 6 — План планировки (подобрана проектировщиком, плана заказчика нет) л. 30 — План потолков	Высота до плиты 2745 мм — по отметке +2.745 плана потолков (К-2).	Решение автора: от чистого пола до плиты 2650 мм; отметки плана −95 мм, перепады сохранены: по плите +2.650, комнаты +2.590, прихожая +2.550, санузел и ванная +2.505. Датум отметок плана — допущение (отдельный вопрос).	Утверждено: Кырлан А.С., 03.11.2026. Предложил: Александр Кырлан, решение автора.
ИЗ-2	03.11.2026	л. 12 — План размещения мебели и оборудования	Назначение помещений не подписано (К-11).	Решение автора — по предложению исполнителя: кабинет у окна (бра 12), кухня-столовая с эркером (подсветка 13), гостиная, спальня (подвесы 13-А/13-Б, кровать 1800 между ними).	Утверждено: Кырлан А.С., 03.11.2026. Предложил: Александр Кырлан, решение автора.
ИЗ-3	03.11.2026	л. 17 — План выводов сантехники л. 44 — Раскладка плитки. Планы полов	Ванная и санузел не подписаны (К-12).	Решение автора: большее — ванная (ванна 1700 у правой стены, умывальник на тумбе 800, стиральная машина 600 × 600 с выводами и розеткой на своей группе); меньшее — санузел (подвесной унитаз, гигиенический душ, раковина 400).	Утверждено: Кырлан А.С., 03.11.2026. Предложил: Александр Кырлан, решение автора.
ИЗ-4	03.11.2026	полный альбом	Несущие стены не известны (К-13).	Решение автора: все существующие стены — несущие до техзаключения; демонтаж и штробление — после него.	Утверждено: Кырлан А.С., 03.11.2026. Предложил: Александр Кырлан, решение автора.
ИЗ-5	03.11.2026	л. 38 — План освещения л. 30 — План потолков	Споты 70 мм в 60 мм запотолочного (К-31).	Решение: встраиваемые светильники тонкие, монтажная глубина ≤ 50 мм; марки исходного плана сохранены; тип — в спецификации с пометкой «глубина ≤ 50 мм».	Утверждено: Кырлан А.С., 03.11.2026. Предложил: Александр Кырлан, решение автора.
ИЗ-6	03.11.2026	л. 41 — План вентиляции	Вентилятор 11 в потолке мокрых: 145 < 150 мм (К-32).	Решение: вытяжная решётка на стене санузла и ванной в канал, вентилятор канальный настенный с обратным клапаном; знак 11 плана — не в потолке.	Утверждено: Кырлан А.С., 03.11.2026. Предложил: Александр Кырлан, решение автора.
ИЗ-7	03.11.2026	л. 6 — План планировки (подобрана проектировщиком, плана заказчика нет)	Датум отметок плана не известен (К-30).	Решение: допущение сохраняется — отметки дизайнера на 95 мм ниже чистого пола; подтвердить на обмере (не блокирует выпуск).	Утверждено: Кырлан А.С., 03.11.2026. Предложил: Александр Кырлан, решение автора.


Примечания

1. Номера листов — по ведомости рабочих чертежей комплекта (лист «Общие данные»).
2. Графа «Если решения нет» показывает состояние решения на листах; влияние на сроки и стоимость по пунктам не оценивалось.
3. Пункт, по которому принято решение, при следующем выпуске комплекта из таблиц исключается.


					Проект: Квартира 68 м², элитный модерн			
	Лист	№ док.	Подпись	Дата	Открытые вопросы, принятые допущения и конфликты. Лист 3 из 3	Стадия	Лист	Листов
Дизайнер	Кырлан А.С.			04.11.26		П	78	86

Правка к этому листу


Вид с фасадами

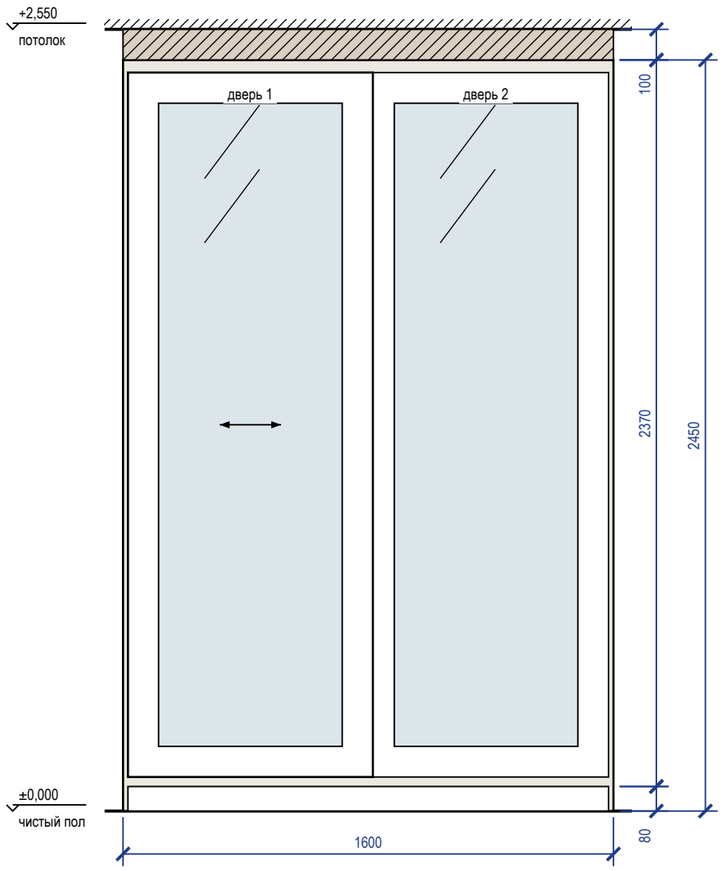


Вид без фасадов

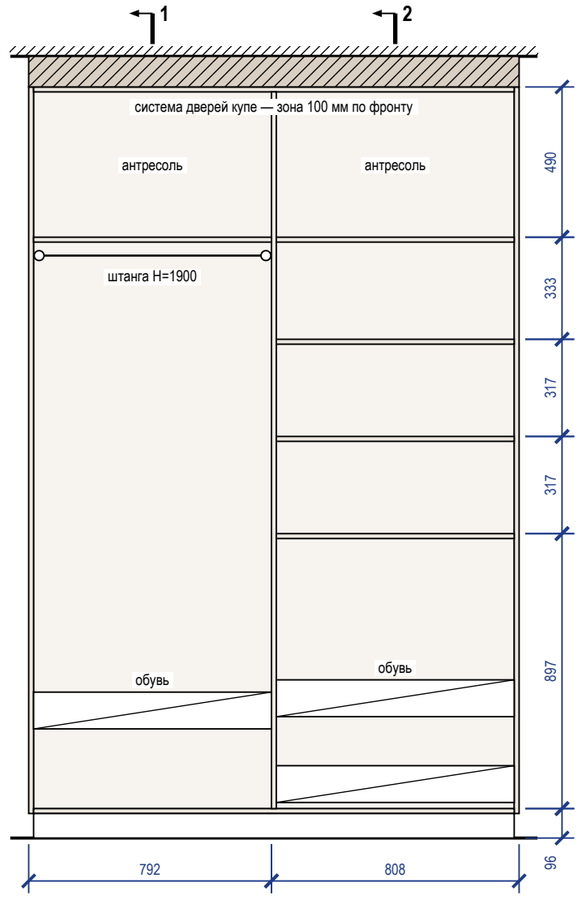

Разрез 1-1

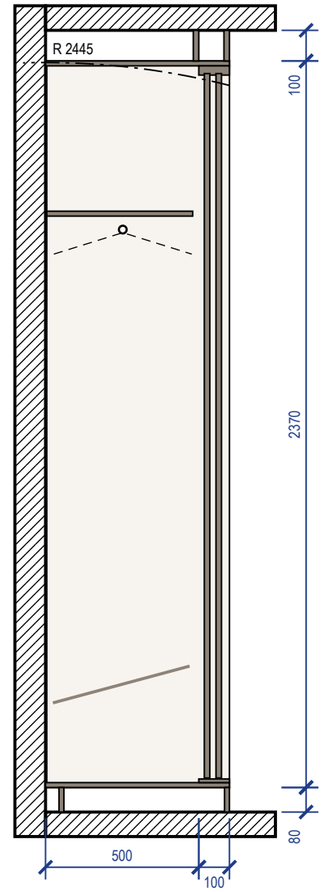


Разрез 2-2

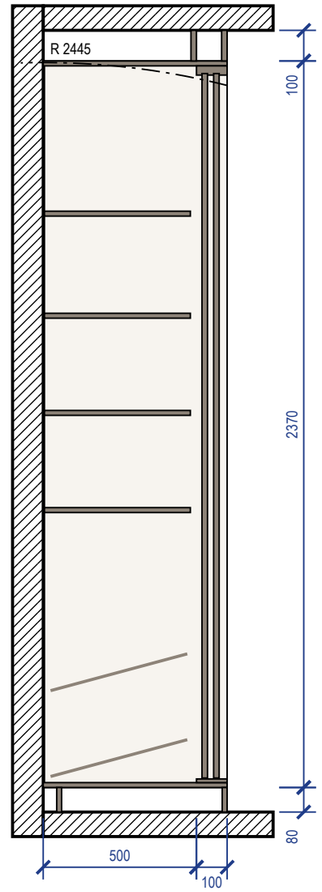

Примечания

1. Размеры — в мм по чистовой отделке; изделие 1600×600×2450 (Ш×Г×В). Перед раскроем — контрольный замер цеха после чистовой отделки стен, пола и потолка.
2. Корпус — ЛДСП 16 мм, задняя стенка ХДФ 4 мм в паз, цоколь 80 мм на регулируемых опорах; двери купе — МДФ, шпон / эмаль 18 мм; вставка — зеркало серебро 4 мм на безопасной плёнке, в профиле двери; нахлёст 30 мм, ширина двери 799 мм, высота — проём минус 40 мм; цвет — по колерной карте.
3. Кромка: скрытые торцы 0,4 мм, видимые 1 мм (ПВХ/АБС).
4. Номинальные зазоры: дверь купе — боковина 3 мм, фасад ящика — стойка 2 мм; ящики внутри купе — с накладкой 30 мм на стойке со стороны нахлёста дверей.
5. Присадка по 32-й системе — выполняет цех.
6. Компенсатор 100 мм — короб из ЛДСП по фронту и торцам, подгоняется к потолку при монтаже (припуск 20 мм), крепится к корпусу и к потолку.
7. Подъём корпуса: диагональ боковины без цоколя $\sqrt{(2370^2 + 600^2)} = 2445$ мм < 2550 мм до потолка — корпус собирается лёжа, поднимается поворотом и ставится на цоколь.
8. Крепление к стене от опрокидывания — уголки 2 шт. к несущему основанию (монтажная схема шкафов).


3D орто

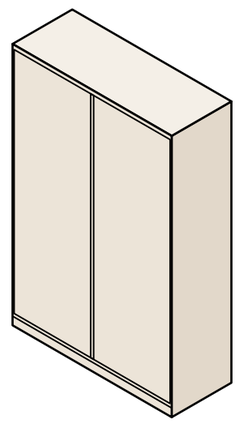


					Проект: Квартира 68 м², элитный модерн	**М 1:20**
	Лист	№ док.	Подпись	Дата		
Дизайнер	Кырлан А.С.			04.11.26	Шкаф-купе М_03	Стадия: П; Лист: Д_1; Листов: 86

выпуск 04.11.2026 № f0db2de63c · стр. 79 из 86


Вид с фасадами

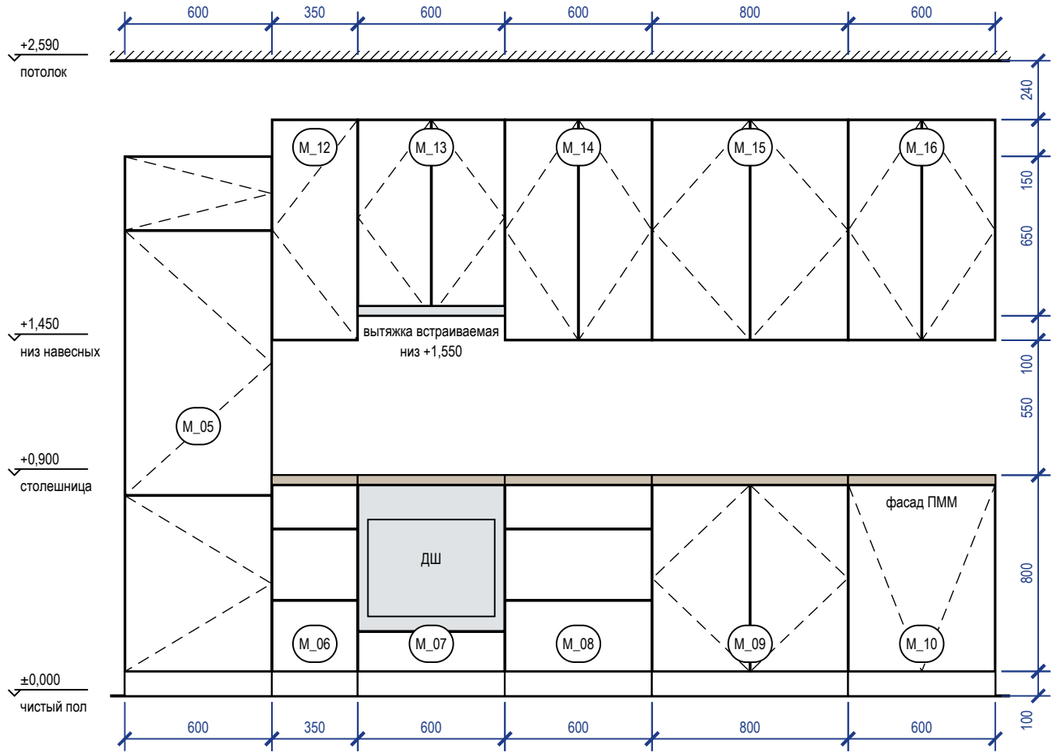


Вид без фасадов (наполнение, выводы)

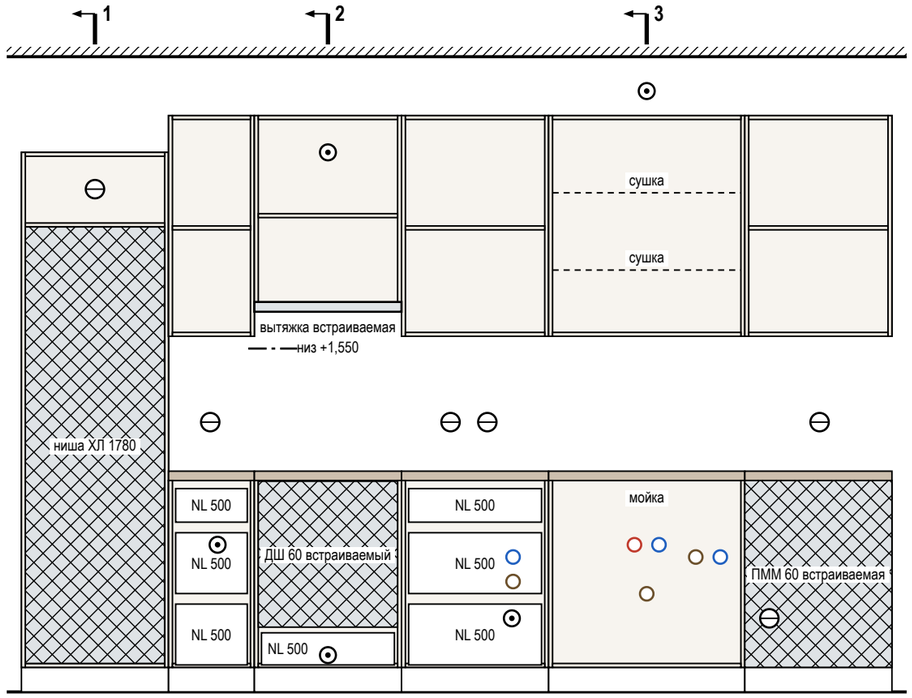


Разрез 1-1

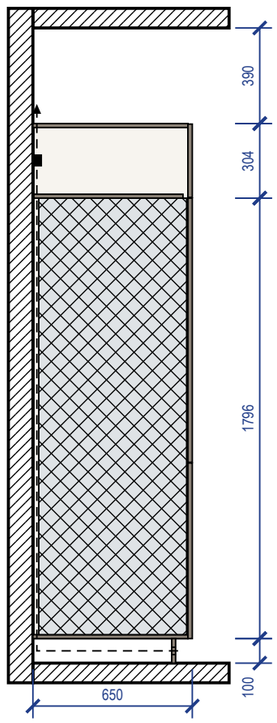


Разрез 2-2

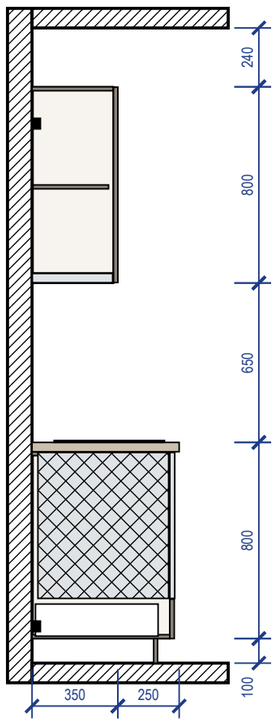

Разрез 3-3

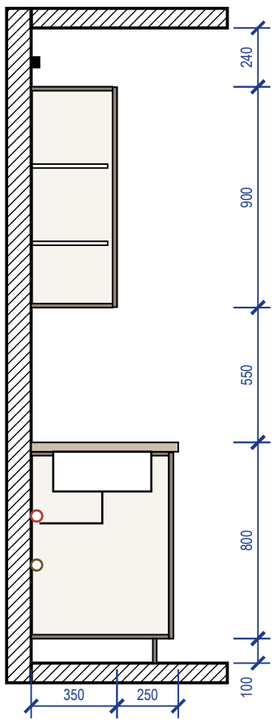

3D орто

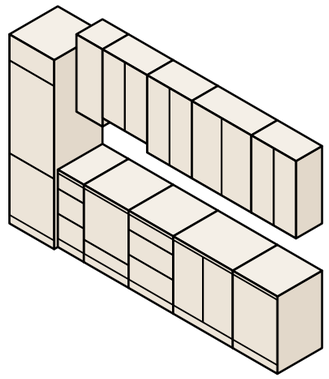

Примечания

1. Размеры — в мм по чистовой отделке, вид из помещения; марки — как на плане расстановки. Перед раскроем — контрольный замер цеха после фартука и пола.
2. Корпуса — ЛДСП 16 мм, задняя стенка ХДФ 4 мм; фасады — МДФ: шпон американского ореха (нижние модули) и эмаль пыльно-синяя с узкой филёнкой (колонны), латунные ручки-скобы 18 мм, цвет по колерной карте; столешница 38 мм, свес 20 мм; цоколь 100 мм.
3. Кромка: скрытые торцы 0,4 мм, видимые 1 мм. Номинальные зазоры: между фасадами 3 мм, фасад — столешница 3 мм, фасад — стена не менее 3 мм.
4. Ящики полного выдвижения и петли — с доводчиком; присадка по 32-й системе — выполняет цех.
5. Вытяжка встраивается в дно навесного модуля M_13 над варочной: её низ на 1550 мм от пола, 650 мм над панелью (не меньше 650 мм).
6. Ниши техники (холодильник — ориентир 1780 мм) — по монтажным схемам выбранных моделей: решётка в цоколе и канал за пеналом холодильника, зазор за духовым шкафом, фасад ПММ на двери машины.

					Проект: Квартира 68 м², элитный модерн		M 1:25
	Лист	№ док.	Подпись	Дата	Кухня (пом. 5). Развёртка гарнитура	Стадия	Лист	Листов
Дизайнер	Кырлан А.С.			04.11.26		П	Д_2	86

Ведомость отделки помещений (форма 1 прил. А ГОСТ 21.501-2018). Лист 1 из 2

№	Наименование помещения	Потолок			Стены и перегородки			Низ стен (плинтус)			Пол		Примечание
		Вид отделки	Код цвета	S, м²	Вид отделки	Код цвета	S, м²	Вид отделки	Код цвета	L, м	Вид отделки	S, м²	
1	Кабинет 10,61 м²	ГКЛ по каркасу П113, отм. +2,590; окраска, Tikkurila Euro Power 7, глубокоматовая, 2 слоя, подготовка Q3	Tikkurila G503	10,61	Окраска, Farrow & Ball Modern Emulsion, матовая, 2 слоя, подготовка Q3 Акцент — стена B: окраска, Tikkurila Euro Power 7, колеровка по NCS, матовая, 2 слоя, подготовка Q3	Farrow & Ball No. 2003 Farrow & Ball No. 30	20,12 9,60	Плинтус МДФ h=80 мм, аналог: МДФ под покраску 80×16	Farrow & Ball No. 2003	12,3	Аналог: инженерная доска, дуб натуральный, масло, 1-полосная, 14/4 мм, на клею; тип 1, отм. ЧП ±0,000	10,61	Н стен 2590 (до потолка); плинтус в цвет: стены
2	Санузел 1,85 м²	ГКЛВ по каркасу П113, отм. +2,505; окраска, Tikkurila Euro Power 7, матовая, 2 слоя, подготовка Q3	Tikkurila G503	1,85	Облицовка плиткой, аналог: керамогранит под травертин, матовый, 600×1200×9 мм, клей C2 TE S1, затирка CG2WA	по артикулу	11,76	нет			Аналог: керамогранит ректифицированный под травертин, матовый, 600×600×9 мм; тип 2, отм. ЧП −0,015	1,85	Н стен 2520 (до потолка); тёплый пол; гидроизоляция обмазочная, 2 слоя, с заведением на стены 200 мм (по пирогу пола); тест проливом и акт скрытых работ
3	Ванная 3,96 м²	ГКЛВ по каркасу П113, отм. +2,505; окраска, Tikkurila Euro Power 7, матовая, 2 слоя, подготовка Q3	Tikkurila G503	3,96	Облицовка плиткой, аналог: керамогранит под травертин, матовый, 600×1200×9 мм, клей C2 TE S1, затирка CG2WA	по артикулу	17,72	нет			Аналог: керамогранит ректифицированный под травертин, матовый, 600×600×9 мм; тип 2, отм. ЧП −0,015	3,96	Н стен 2520 (до потолка); тёплый пол; гидроизоляция обмазочная, 2 слоя, с заведением на стены 200 мм; над ванной — до 2000 и 300 мм за борт (по пирогу пола); тест проливом и акт скрытых работ
4	Прихожая 13,87 м²	ГКЛ/Существующий потолок по каркасу П113, отм. +2,550; +2,650; окраска, Tikkurila Euro Power 7, глубокоматовая, 2 слоя, подготовка Q3	Tikkurila G503	13,87	Окраска, Farrow & Ball Modern Emulsion, матовая, 2 слоя, подготовка Q3	Farrow & Ball No. 2003	27,58	Плинтус МДФ h=80 мм, аналог: МДФ под покраску 80×16	Farrow & Ball No. 2003	9,8	Аналог: керамогранит ректифицированный под травертин, матовый, 600×1200×9 мм; тип 3, отм. ЧП ±0,000	13,87	Н стен 2550 (до потолка); тёплый пол; матовая моющаяся, класс 1 EN 13300 — осознанно вместо полуматовой; плинтус в цвет: стены
5	Кухня-столовая 12,04 м²	ГКЛ по каркасу П113, отм. +2,590; окраска, Tikkurila Euro Power 7, глубокоматовая, 2 слоя, подготовка Q3	Tikkurila G503	12,04	Окраска, Farrow & Ball Modern Emulsion, матовая, 2 слоя, подготовка Q3 Акцент — стена B: окраска, Tikkurila Euro Power 7, колеровка по NCS, матовая, 2 слоя, подготовка Q3 Фартук кухни (стена A): облицовка керамогранитом, аналог: керамогранит под травертин, матовый, 1200×600×9 мм, клей C2 TE S1, затирка CG2WA	Farrow & Ball No. 2003 Farrow & Ball No. 281 по артикулу	22,56 9,96 1,68	Плинтус МДФ h=80 мм, аналог: МДФ под покраску 80×16	Farrow & Ball No. 2003	13,8	Аналог: инженерная доска, дуб натуральный, масло, 1-полосная, 14/4 мм, на клею; тип 1, отм. ЧП ±0,000	12,04	Н стен 2590 (до потолка); матовая моющаяся, класс 1 EN 13300 — осознанно вместо полуматовой; плинтус в цвет: стены
6	Гостиная 12,24 м²	ГКЛ по каркасу П113, отм. +2,590; окраска, Tikkurila Euro Power 7, глубокоматовая, 2 слоя, подготовка Q3	Tikkurila G503	12,24	Окраска, Farrow & Ball Modern Emulsion, матовая, 2 слоя, подготовка Q3 Акцент — стена A: окраска, Farrow & Ball Modern Emulsion, матовая, 2 слоя, подготовка Q3	Farrow & Ball No. 2003 Farrow & Ball No. 43	22,36 9,92	Плинтус МДФ h=80 мм, аналог: МДФ под покраску 80×16	Farrow & Ball No. 2003	13,3	Аналог: инженерная доска, дуб натуральный, масло, 1-полосная, 14/4 мм, на клею; тип 1, отм. ЧП ±0,000	12,24	Н стен 2590 (до потолка); плинтус в цвет: стены
7	Спальня 13,90 м²	ГКЛ по каркасу П113, отм. +2,590; окраска, Tikkurila Euro Power 7, глубокоматовая, 2 слоя, подготовка Q3	Tikkurila G503	13,90	Окраска, Farrow & Ball Modern Emulsion, матовая, 2 слоя, подготовка Q3 Акцент — стена B: окраска, Farrow & Ball Modern Emulsion, матовая, 2 слоя, подготовка Q3	Farrow & Ball No. 2003 Farrow & Ball No. 34	23,37 12,95	Плинтус МДФ h=80 мм, аналог: МДФ под покраску 80×16	Farrow & Ball No. 2003	14,8	Аналог: инженерная доска, дуб натуральный, масло, 1-полосная, 14/4 мм, на клею; тип 1, отм. ЧП ±0,000	13,90	Н стен 2590 (до потолка); плинтус в цвет: стены

Примечания

1. Ведомость продолжена на листе 2 из 2; итоги, сводка площадей и примечания — на последнем листе ведомости.

					Проект: Квартира 68 м², элитный модерн
	Лист	№ док.	Подпись	Дата	Ведомость отделки помещений. Лист 1 из 2
Дизайнер	Кырлан А.С.			04.11.26	

Стадия	Лист	Листов
П	С1	86

Ведомость отделки помещений (форма 1 прил. А ГОСТ 21.501-2018). Лист 2 из 2

№	Наименование помещения	Потолок			Стены и перегородки			Низ стен (плинтус)			Пол		Примечание
		Вид отделки	Код цвета	S, м²	Вид отделки	Код цвета	S, м²	Вид отделки	Код цвета	L, м	Вид отделки	S, м²	
	Итого			**68,47**			**189,56**			**63,9**		**68,47**	

Сводка площадей по материалам отделки

Поверхность	Материал / код цвета	Серия	Площадь, м²
Потолок	Tikkurila G503	Euro Power 7	68,47
Стены	Farrow & Ball No. 2003	Modern Emulsion	115,98
Стены	Farrow & Ball No. 30	Euro Power 7, колеровка по NCS	9,60
Стены	облицовка плиткой 600×1200×9 мм	аналог: керамогранит под травертин, матовый	29,47
Стены	Farrow & Ball No. 281	Euro Power 7, колеровка по NCS	9,96
Стены	Farrow & Ball No. 43	Modern Emulsion	9,92
Стены	Farrow & Ball No. 34	Modern Emulsion	12,95
Фартук	облицовка керамогранитом 1200×600×9 мм	аналог: керамогранит под травертин, матовый	1,68

Примечания

1. Площади поверхностей — по чистым граням стен до отделки: стены = периметр × высоту от чистого пола помещения до низа потолка минус проёмы (облицовка плиткой — до верха облицовки); плинтус = периметр минус дверные проёмы; пол и потолок — по площади помещения. Количество плиток по раскладке. Площади помещений — с учётом всех частей помещения; откосы в площадь стен не входят.
2. Акцентные стены и фартук — отдельными строками, их площадь вычтена из основной отделки стен помещения; фартук — над нижними модулями кухни от столешницы до низа навесных шкафов, где шкафов нет — на 600 мм.
3. Плинтус — длина по периметру за вычетом дверных проёмов; примыкания к наличникам и встроенной мебели — по развёрткам.
4. Формат плитки — Ш×В×Т (ширина × высота в положении укладки × толщина), мм; на полу — вдоль стен А/В × вдоль стен Б/Г.
5. Коды цвета — по веерам производителей; колеровка каждой краски одной партией, проверка выкраса при свете D65 и при лампах проекта.
6. Уровни подготовки Q1–Q4 — система Knauf, не норма ГОСТ/СП; допуски поверхностей — по СП 71.13330.2017 (действующая редакция).
7. «аналог:» — изделие задано характеристиками, марку и артикул согласовать с заказчиком до закупки.

					Проект: Квартира 68 м², элитный модерн
	Лист	№ док.	Подпись	Дата	
Дизайнер	Кырлан А.С.			04.11.26	Ведомость отделки помещений. Лист 2 из 2

Стадия	Лист	Листов
П	С2	86

Поз.	Наименование и техническая характеристика	Тип, марка, обозначение документа	Код продукции	Поставщик	Ед. изм.	Кол.	Образец	Примечание
	Лакокрасочные материалы							
1	Краска интерьерная водно-дисперсионная акриловая для стен, матовая, класс мокрого истирания 1 по EN 13300, база A; цвет по вееру Farrow & Ball No. 2003 «Pointing», колеровка машинная	Farrow & Ball Modern Emulsion		Farrow & Ball	л	32,5		поз. К1 колерной карты; пом. 1, 4, 5, 6, 7; S = 116,0 м² × 2 сл. × 0,12 л/м² = 27,8 л, +10 % и 0,5 л на подкраску → ≥ 31,1 л; тара 6 × 5 л + 1 × 2,5 л
2	Краска интерьерная водно-дисперсионная акриловая для акцентных стен, матовая, класс мокрого истирания 1 по EN 13300, база C; цвет по вееру Farrow & Ball No. 30 «Hague Blue — глубокий сине-зелёный», колеровка машинная	Tikkurila Euro Power 7, колеровка по NCS		Tikkurila	л	5		поз. К2 колерной карты; пом. 1; S = 9,6 м² × 2 сл. × 0,12 л/м² = 2,3 л, +10 % и 0,5 л на подкраску → ≥ 3,0 л; тара 1 × 5 л
3	Краска интерьерная водно-дисперсионная акриловая для потолков, глубокоматовая, класс мокрого истирания 2 по EN 13300, база A; цвет по вееру Tikkurila G503 «Calla», колеровка машинная	Tikkurila Euro Power 7		Tikkurila	л	17,1		поз. К3 колерной карты; пом. 1, 4, 5, 6, 7; S = 62,7 м² × 2 сл. × 0,12 л/м² = 15,0 л, +10 % и 0,5 л на подкраску → ≥ 17,0 л; тара 1 × 9 л + 3 × 2,7 л
4	Краска интерьерная водно-дисперсионная акриловая для потолков, матовая, класс мокрого истирания 1 по EN 13300, база A; цвет по вееру Tikkurila G503 «Calla», колеровка машинная	Tikkurila Euro Power 7		Tikkurila	л	2,7		поз. К5 колерной карты; пом. 2, 3; S = 5,8 м² × 2 сл. × 0,12 л/м² = 1,4 л, +10 % и 0,5 л на подкраску → ≥ 2,0 л; тара 1 × 2,7 л
5	Краска интерьерная водно-дисперсионная акриловая для акцентных стен, матовая, класс мокрого истирания 1 по EN 13300, база C; цвет по вееру Farrow & Ball No. 281 «Stiffkey Blue — чернильный синий», колеровка машинная	Tikkurila Euro Power 7, колеровка по NCS		Tikkurila	л	5		поз. К6 колерной карты; пом. 5; S = 10,0 м² × 2 сл. × 0,12 л/м² = 2,4 л, +10 % и 0,5 л на подкраску → ≥ 3,1 л; тара 1 × 5 л
6	Краска интерьерная водно-дисперсионная акриловая для акцентных стен, матовая, класс мокрого истирания 1 по EN 13300, база C; цвет по вееру Farrow & Ball No. 43 «Eating Room Red — брусничный красный», колеровка машинная	Farrow & Ball Modern Emulsion		Farrow & Ball	л	5		поз. К7 колерной карты; пом. 6; S = 9,9 м² × 2 сл. × 0,12 л/м² = 2,4 л, +10 % и 0,5 л на подкраску → ≥ 3,1 л; тара 1 × 5 л
7	Краска интерьерная водно-дисперсионная акриловая для акцентных стен, матовая, класс мокрого истирания 1 по EN 13300, база C; цвет по вееру Farrow & Ball No. 34 «Calke Green — традиционный шалфей», колеровка машинная	Farrow & Ball Modern Emulsion		Farrow & Ball	л	5		поз. К8 колерной карты; пом. 7; S = 12,9 м² × 2 сл. × 0,12 л/м² = 3,1 л, +10 % и 0,5 л на подкраску → ≥ 3,9 л; тара 1 × 5 л
8	Краска для МДФ и дерева в цвет Farrow & Ball No. 2003 «Pointing» — окраска плинтуса; блеск не ниже блеска стен	марка не задана			л	1,7		поз. К4; пом. 1, 4, 5, 6, 7; L = 63,9 м, S = 6,1 м² × 2 сл. × 0,12 л/м² + 10 %; продукт подобрать в веере Farrow & Ball
9	Грунтовка акриловая под окраску стен и потолков — из системы производителя краски	по системе краски			м²	227		площадь окраски стен, акцентов и потолков; 1 слой перед окраской; расход — по ТУ грунтовки
	Плитка и керамогранит							
10	Керамогранит под травертин, 600×600×9 мм, ректификат, водопоглощение 0,1 % (BIa), противоскольжение R10, PEI IV	аналог по характеристикам			м²	7,56		шов 2 мм; Санузел, пол; Ванная, пол; по раскладке 18 шт (S = 5,81 м²), с запасом 21 шт
11	Керамогранит под травертин, 600×1200×9 мм, ректификат, водопоглощение 0,1 %	аналог по характеристикам			м²	43,92		шов 2 мм; Санузел, стены А–Г; Санузел, короб инсталляции; Ванная, стены А–Г; по раскладке 52 шт (S = 30,23 м²), с запасом 61 шт
12	Керамогранит ректифицированный под травертин, матовый, 600×1200×9 мм, водопоглощение 0,1 % (BIa), противоскольжение R10, PEI IV	аналог по характеристикам			м²	19,44		шов 2 мм; Прихожая, пол; по раскладке 24 шт (S = 13,87 м²), с запасом 27 шт
13	Керамогранит под травертин, матовый, 1200×600×9 мм, ректификат, водопоглощение 0,1 % (BIa)	аналог по характеристикам			м²	4,32		шов 2 мм; Кухня-столовая, фартук (ст. А); по раскладке 5 шт (S = 1,68 м²), с запасом 6 шт
	Напольные покрытия							
14	Инженерная доска, дуб натуральный, масло, 1-полосная, 14/4 мм, эмиссия E1, укладка на клей	аналог по характеристикам			м²	52,3		пом. 1, 5, 6, 7; S = 48,79 м² + 7 % (прямая укладка); к заказу — кратно упаковке
15	Клей для паркета и инженерной доски, эластичный (СМП / полиуретановый)	по рекомендации производителя доски			м²	49		площадь приклейки; расход и шпатель — по ТУ клея
	Погонажные изделия							
16	Плинтус МДФ под покраску 80×16, крепление к стене, окраска в цвет Farrow & Ball No. 2003	аналог по характеристикам			м	71		пом. 1, 4, 5, 6, 7; L = 63,9 м (периметр без дверных проёмов) + 10 % на подрезку; в штуках — по длине планки
	Смеси и материалы для облицовки							
17	Затирка для швов плитки, класс CG2WA по EN 13888	Mapei Ultracolor Plus 132		Mapei	кг	4,1		по раскладке (a+b)/(a·b) × шов × t × 1,6 + 10 %; в т. ч. 0,1 кг — позиции раскладки без марки
18	Клей плиточный C2 TE S1 по EN 12004, слой 5 мм	Ceresit CM 17		Ceresit	кг	411		17 меш. по 25 кг; 1,5 кг/м² на 1 мм слоя + 10 %; в т. ч. 14 кг — позиции раскладки без марки
19	Гидроизоляция обмазочная мокрых зон: пол, стены по периметру, зоны замачивания; 2 слоя с армирующей лентой в углах	аналог по характеристикам			м²	15,8		площадь по листу раскладки плитки + 10 %; расход смеси — по ТУ
20	Лента демпферная по периметру пола из плитки	аналог по характеристикам			м	26,9		периметр без дверных проёмов + 10 %

Примечания

1. Количества — из геометрии проекта: площади поверхностей по чистым граням стен до отделки (те же, что в ведомости отделки и колерной карте), плитка, клей и затирка — по раскладке плиточника; в графе «Кол.» — к заказу, с запасом.
2. Краска: расход 0,12 л/м² на слой в 2 слоя, если по ТУ не задан иной; запас 10 % и 0,5 л на подкраску каждого кода. Один код — одна партия, колеровка машинная в колеровочном центре бренда; в заказ — только после утверждения выкраса (колерная карта). Фасовка — по каталогу бренда на дату выпуска; к заказу — не меньше расчётного объёма.
3. «Аналог по характеристикам» — допускается изделие другого производителя с характеристиками не ниже указанных, по согласованию с автором проекта.
4. Графы «Код продукции» и «Масса 1 ед.» не заполнены: коды по классификатору продукции не присвоены, масса единицы до 25 кг (ГОСТ 21.110-2013).
5. Грунтовка и клей для доски указаны площадью обработки; объём — по ТУ выбранного продукта.

					Проект: Квартира 68 м², элитный модерн
	Лист	№ док.	Подпись	Дата	
Дизайнер	Кырлан А.С.			04.11.26	Спецификация отделочных материалов

Стадия	Лист	Листов
П	С3	86

выпуск 04.11.2026 № f0db2de63c · стр. 83 из 86

Список покупок: материалы для магазина

№	Что купить	Артикул или характеристика	Нужно с запасом	Брать в магазине	Фасовка	Уточнить в магазине	Помещения	Кто покупает
Покрытия полов и облицовка								
1	Инженерная доска (дуб натуральный, рабочий слой 4 мм, эмиссия E1, прямая укладка)	по характеристике: инженерная доска, дуб натуральный, масло, 1-полосная, 14/4 мм	52,45 м²	52,5 м²		уточнить в магазине: м² в упаковке	1, 5, 6, 7	по проекту
2	Клей для паркетной и инженерной доски (эластичный, по ТУ изготовителя доски)	на выбор бригады по проекту	49,02 м²			уточнить в магазине: расход и фасовку — по выбранному продукту		бригада
3	Керамогранит 600×600 мм под травертин	по характеристике: керамогранит под травертин	20 шт	21 шт		уточнить в магазине: штук в коробке	2, 3	по проекту
4	Керамогранит 600×1200 мм под травертин	по характеристике: керамогранит под травертин	58 шт	61 шт		уточнить в магазине: штук в коробке	2, 3	по проекту
5	Керамогранит 600×1200 мм ректифицированный под травертин, матовый	по характеристике: керамогранит ректифицированный под травертин, матовый	27 шт	27 шт		уточнить в магазине: штук в коробке	4	по проекту
6	Керамогранит 1200×600 мм под травертин, матовый	по характеристике: керамогранит под травертин, матовый	6 шт	6 шт		уточнить в магазине: штук в коробке	5	по проекту
Сухие смеси и гидроизоляция								
7	Клей плиточный цементный класса C2 TE S1 (ГОСТ Р 56387-2018)	Ceresit CM 17 или аналог	410,97 кг	17 меш.	мешок 25 кг			по проекту
8	Затирка цементная класса CG2WA, цвет — по колерной карте	Mapei Ultracolor Plus 132 или аналог	4,08 кг	3 упак.	упак. 2 кг			по проекту
9	Гидроизоляция обмазочная полимерная, 2 слоя, лента в углах, манжеты на выводах	на выбор бригады по проекту	15,75 м²			уточнить в магазине: расход и фасовку — по выбранному продукту	2, 3	бригада
10	Лента демпферная по периметру пола из плитки	на выбор бригады по проекту	26,85 м	27 м		уточнить в магазине: фасовку		бригада
11	Смесь цементно-песчаная для стяжки М200 (50 мм, 33 мм)	на выбор бригады по проекту	3,53 м³			уточнить в магазине: расход и фасовку — по выбранному продукту		бригада
12	Смесь штукатурная гипсовая для машинного и ручного нанесения по маякам, слой до 10 мм	на выбор бригады по проекту	210,27 м²			уточнить в магазине: расход и фасовку — по выбранному продукту	1, 2, 3, 4, 5, 6, 7	бригада
Короба из ГКЛВ								
13	Лист ГКЛВ 12,5 мм, 2500 × 1200 мм, обшивка коробов в 2 слоя	на выбор бригады по проекту	3,23 м²	2 лист.	лист 3,00 м²		2	бригада
14	Профиль стальной оцинкованный 27 × 28 мм: каркас коробов (стойки и направляющие)	на выбор бригады по проекту	7,7 м	3 шт	хлыст 3 м			бригада
Слаботочные сети								
15	Кабель домофона — тип по системе поставщика	на выбор бригады по проекту	3,1 м	4 м		уточнить в магазине: длину бухты		бригада
16	Кабель коаксиальный RG-6 (75 Ом) к розеткам ТВ	на выбор бригады по проекту	14,1 м	15 м		уточнить в магазине: длину бухты		бригада
17	Кабель U/UTP кат. 5e (LAN, Wi-Fi и камеры по PoE)	на выбор бригады по проекту	27,4 м	28 м		уточнить в магазине: длину бухты		бригада
18	Кабель U/UTP кат. 6 (LAN, Wi-Fi и камеры по PoE)	на выбор бригады по проекту	2,7 м	3 м		уточнить в магазине: длину бухты		бригада
19	Гофротруба Ø20 для слаботочных линий, отдельно от силовых	на выбор бригады по проекту	42,6 м	43 м		уточнить в магазине: длину бухты		бригада
20	Розетка компьютерная RJ45, кат. 6, с рамкой и подрозетником	на выбор бригады по проекту	2 шт	2 шт	шт			бригада
21	Розетка телевизионная (коаксиальная) с рамкой и подрозетником	на выбор бригады по проекту	1 шт	1 шт	шт			бригада
22	Трубка или монитор домофона (поставка домофонной организации)	на выбор бригады по проекту	1 шт	1 шт	шт			по проекту

					Проект: Квартира 68 м², элитный модерн		
	Лист	№ док.	Подпись	Дата	Список покупок	Стадия	Лист	Листов
Дизайнер	Кырлан А.С.			04.11.26		П	С4	86

Список покупок: материалы для магазина (продолжение)

№	Что купить	Артикул или характеристика	Нужно с запасом	Брать в магазине	Фасовка	Уточнить в магазине	Помещения	Кто покупает
23	Щит слаботочный ЩС: корпус, DIN-рейка, розетки 220 В	на выбор бригады по проекту	1 шт	1 шт	шт			бригада
24	Патч-панель, портов не менее 3	на выбор бригады по проекту	1 шт	1 шт	шт			бригада
Лакокрасочные материалы								
25	Краска интерьерная акриловая, матовая, класс истирания 1	Tikkurila Euro Power 7, колеровка по NCS No. 30 «Hague Blue глубокий сине-зелёный»	2,53 л	1 банк.	банка 2,7 л		1	по проекту
26	Краска интерьерная акриловая, матовая, класс истирания 1	Farrow & Ball Modern Emulsion No. 2003 «Pointing»	30,62 л	13 банк.	банка 2,5 л		1, 4, 5, 6, 7	по проекту
27	Краска интерьерная акриловая, глубокоматовая, класс истирания 2	Tikkurila Euro Power 7 G503 «Calla»	16,54 л	7 банк.	банка 2,7 л		1, 4, 5, 6, 7	по проекту
28	Краска интерьерная акриловая, матовая, класс истирания 1	Tikkurila Euro Power 7 G503 «Calla»	1,53 л	1 банк.	банка 2,7 л		2, 3	по проекту
29	Краска интерьерная акриловая, матовая, класс истирания 1	Tikkurila Euro Power 7, колеровка по NCS No. 281 «Stiffkey Blue — чернильный синий»	2,63 л	1 банк.	банка 2,7 л		5	по проекту
30	Краска интерьерная акриловая, матовая, класс истирания 1	Farrow & Ball Modern Emulsion No. 43 «Eating Room Red брусничный красный»	2,62 л	2 банк.	банка 2,5 л		6	по проекту
31	Краска интерьерная акриловая, матовая, класс истирания 1	Farrow & Ball Modern Emulsion No. 34 «Calke Green — традиционный шалфей»	3,42 л	2 банк.	банка 2,5 л		7	по проекту
32	Шпаклёвка финишная полимерная под окраску (стены и потолки, Q3)	на выбор бригады по проекту	249,58 м²			уточнить в магазине: расход и фасовку — по выбранному продукту		бригада
33	Грунтовка акриловая глубокого проникновения, 2 слоя	на выбор бригады по проекту	285,58 м²			уточнить в магазине: расход и фасовку — по выбранному продукту		бригада
Погонажные изделия и потолки								
34	Плинтус напольный МДФ под покраску, h=80 мм, крепление к стене	по характеристике: плинтус МДФ под покраску 80×16	70,28 м.п.	30 шт	хлыст 2,4 м		1, 4, 5, 6, 7	по проекту
35	Потолок подвесной ГКЛ/ГКЛВ по каркасу Knauf П113: листы, профили, подвесы, лента, шпаклёвка швов	Knauf П113	68,04 м²			уточнить в магазине: расход и фасовку — по выбранному продукту		по проекту
Инженерные изделия								
36	Мат нагревательный электрический для тёплого пола под плитку, с холодным концом и муфтой	на выбор бригады по проекту	3 м²			уточнить в магазине: расход и фасовку — по выбранному продукту	3, 4	по проекту
37	Терморегулятор тёплого пола с выносным датчиком пола, монтаж в подрозетник	на выбор бригады по проекту	2 шт	2 шт	шт			по проекту

Примечания

1. «Нужно с запасом» — расход по чертежам и раскладке плюс запас на подрезку и подкраску; «Брать в магазине» — то же количество в единицах, которыми продают (банки, мешки, упаковки, листы, штуки, литры).
2. «Уточнить в магазине» — фасовки этого товара в проекте нет: спросите у продавца, сколько в упаковке, и возьмите целое число упаковок не меньше «Нужно с запасом».
3. Плитку, доску и краску одного цвета берите одной партией (один калибр и тон на помещение) и сохраните чек и номер партии до конца ремонта.
4. «По характеристике» — артикул не выбран: подойдёт любой товар с этими свойствами, согласуйте его с дизайнером до покупки. «Бригада» материал выбирает и закупает бригада по своей технологии.
5. Помещения: 1 — Кабинет; 2 — Санузел; 3 — Ванная; 4 — Прихожая; 5 — Кухня-столовая; 6 — Гостиная; 7 — Спальня; «—» — материал для нескольких помещений, расход по месту.


выпуск 04.11.2026 № f0db2de63c · стр. 85 из 86

					Проект: Квартира 68 м², элитный модерн
	Лист	№ док.	Подпись	Дата	Список покупок (окончание)
Дизайнер	Кырлан А.С.			04.11.26	

Стадия	Лист	Листов
П	С5	86


1 Порог 15 мм: мокрая зона — смежное помещение (М 1:5)

Применение: двери Д-2, Д-3

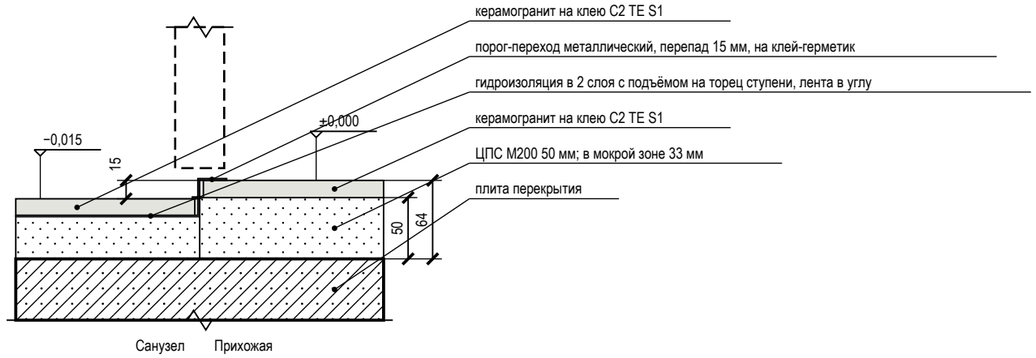


2 Короб стояков К1-1 с люком и звукоизоляцией (М 1:20)

Применение: пом. 3

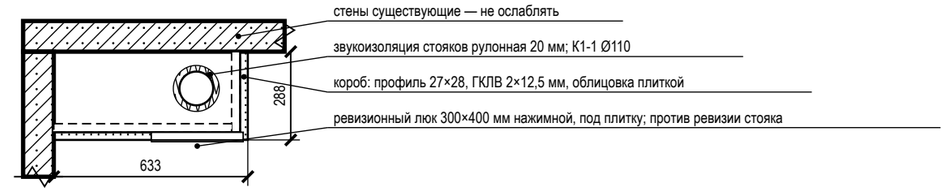


3 Гидроизоляция санузла: заход на стены 200 мм, примыкание ванны (М 1:20)

Применение: пом. 2, 3

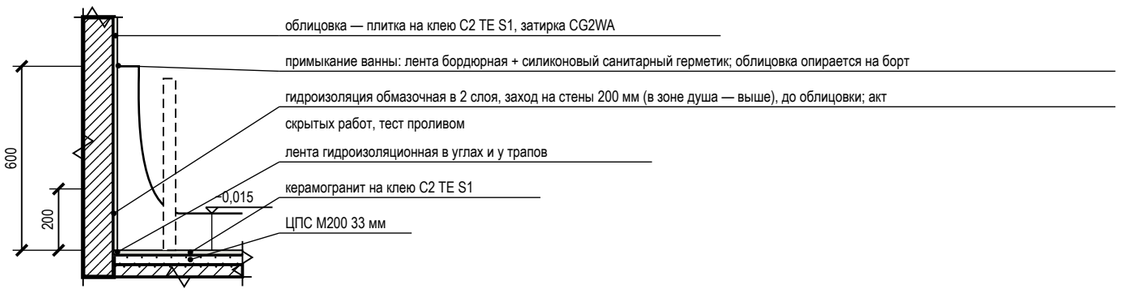


4 Плинтус МДФ 80×16 мм у окрашенной стены по доске (ламинату) (М 1:10)

Применение: пом. 1, 5, 6, 7

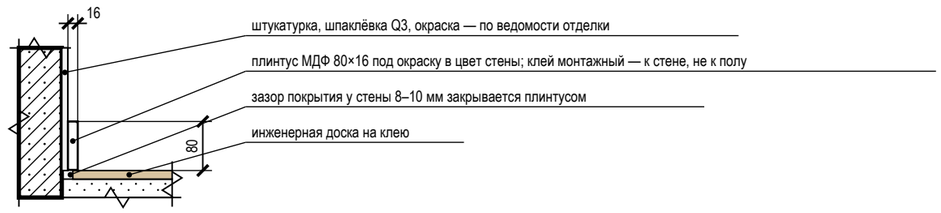

5 Плинтус МДФ 80×16 мм у окрашенной стены по керамограниту (плитке) (М 1:10)

Применение: пом. 4

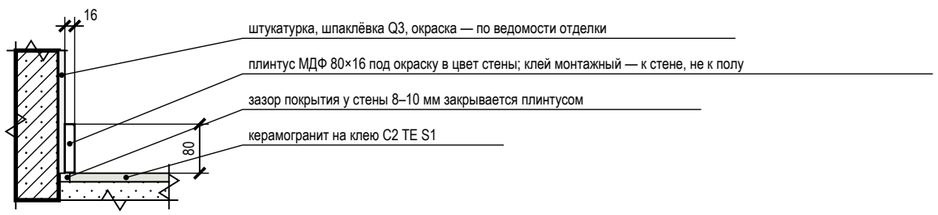

Условные обозначения

- железобетон (плита, стены) — условно: конструкция не установлена
- кладка, перегородка — условно: конструкция не установлена
- стяжка, раствор
- гипсокартон ГКЛВ
- звукоизоляция, эластичный заполнитель
- плитка, керамогранит на клею
- инженерная доска (покрытие пола)
- металлический профиль (порог, Т-профиль, короб двери)
- гидроизоляция (обмазочная, лента)

Примечания

1. Узлы — типовые решения проекта для мест, отмеченных выносками на листе схемы расположения развёрток и узлов; размеры — в мм, отметки — в м от ±0,000.
2. Узлы с гидроизоляцией, закладными и коробами скрытого монтажа принимаются по актам скрытых работ до закрытия отделкой; гидроизоляция — после теста проливом (24 ч).
3. Марки изделий (порог, Т-профиль, короб скрытой двери, люк) — по спецификациям; замена — на аналог с теми же габаритами по согласованию с автором проекта.
4. Материал плиты перекрытия и стен в узлах показан условно (железобетон, кладка): конструкция дома не установлена — крепёж, анкеры и толщины слоёв уточняются после обследования (до него — по допущениям общих указаний).

	Лист	№ док.	Подпись	Дата
Дизайнер	Кырлан А.С.			04.11.26

Проект: Квартира 68 м², элитный модерн

Узлы	Стадия	Лист	Листов
	П	С6	86

выпуск 04.11.2026 № f0db2de63c · стр. 86 из 86