L

LINEA

ДИЗАЙН-ПРОЕКТ ИНТЕРЬЕРА

# Квартира 55 м²

*кухня-гостиная и спальня*



Визуализация кухни-гостиной · 3D

| ОБЩАЯ ПЛОЩАДЬ | ПОМЕЩЕНИЙ | СТАДИЯ | ШИФР | ОСНОВА |
|---|---|---|---|---|
| 55,23 м² | 6, из них жилых 2 | Рабочий проект · предварительно | ГД-2026-006-АИ | план заказчика, без обмера |

ПАЛИТРА ОТДЕЛКИ

| NCS S 1502-Y50 | NCS S 1002-Y50 | V503 |
|---|---|---|
| 44 % | 32 % | 24 % |

АВТОР ПРОЕКТА

Кырлан Александр Сергеевич

Ноябрь 2026

| Изм. | Кол.уч | Лист | № док. | Подп. | Дата | ГД-2026-006-АИ | | |
|---|---|---|---|---|---|---|---|---|
| | | | | | | Квартира 58 м² | | |
| | | | | | | Общая площадь 55,23* м² · * размеры приняты, не замерены (реестр — л. 6, 7, К-5) | | |
| Разраб. | | Кырлан А.С. | | | 04.11.26 | Дизайн-проект интерьера | Стадия | Лист | Листов |
| Пров. | | | | | | | РП | 1 | 87 |
| ГИП | | | | | | | | | |
| | | | | | | Титульный лист | Кырлан Александр Сергеевич | | |
| Н. контр. | | | | | | М б/м | | | |
| Утв. | | | | | | | | | |

выпуск 04.11.2026 № 3da8f16a26 · стр. 1 из 96

# Общие данные

Комплект ГД-2026-006-АИ · Квартира 58 м² · кухня-гостиная и спальня

Допущения и предложения на листе. См. лист открытых вопросов (листы 6, 7).

### Ведомость рабочих чертежей основного комплекта ГД-2026-006-АИ

| Лист | Наименование | Примечание |
|---|---|---|
| 1 | Титульный лист | |
| 2 | Общие данные | |
| 3 | Общие данные | |
| 4 | Общие данные | |
| 5 | Общие данные | |
| 6 | Открытые вопросы, принятые допущения и конфликты. Лист 1 из 2 | |
| 7 | Открытые вопросы, принятые допущения и конфликты. Лист 2 из 2 | |
| 8 | Задание на контрольный обмер и обследование. Лист 1 из 3 | |
| 9 | Задание на контрольный обмер и обследование. Лист 2 из 3 | |
| 10 | Задание на контрольный обмер и обследование. Лист 3 из 3 | |
| 11 | График закупок и работ. Лист 1 из 3 | |
| 12 | График закупок и работ. Лист 2 из 3 | |
| 13 | График закупок и работ. Лист 3 из 3 | |
| 14 | Обмерный план | |
| 15 | План демонтажа и монтажа перегородок | |
| 16 | План дверей и ведомость заполнения проёмов | |
| 17 | Концепция интерьера | |
| 18 | План расстановки мебели | |
| 19 | Спецификация мебели и оборудования | |
| 20 | План розеток и электровыводов | |
| 21 | План освещения | |
| 22 | План выключателей и схема включения | |
| 23 | Ведомость электроточек и изделий | |
| 24 | Однолинейная схема щита | |
| 25 | План принципиальных трасс | |
| 26 | План слаботочных сетей | |
| 27 | План вентиляции | |
| 28 | План отопления | |
| 29 | План выводов сантехники | |
| 30 | Схема разводки водопровода и канализации | |

### Ведомость рабочих чертежей основного комплекта ГД-2026-006-АИ (продолжение)

| Лист | Наименование | Примечание |
|---|---|---|
| 31 | Аксонометрическая схема В1 (холодное водоснабжение) | |
| 32 | Аксонометрическая схема Т3 (горячее водоснабжение) | |
| 33 | Аксонометрическая схема К1 (канализация) | |
| 34 | Развёртки мокрых зон: выводы ВК. Кухня-гостиная | |
| 35 | Развёртки мокрых зон: выводы ВК. Ванная (лист 1 из 2) | |
| 36 | Развёртки мокрых зон: выводы ВК. Ванная (лист 2 из 2) | |
| 37 | Развёртки мокрых зон: выводы ВК. Санузел | |
| 38 | Спецификация сантехнического оборудования | |
| 39 | Техническое задание на подбор светильников | |
| 40 | План потолков | |
| 41 | Разрезы и узлы потолков | |
| 42 | Разрезы и узлы потолков (продолжение) | |
| 43 | Раскладка плитки. Планы полов | |
| 44 | Раскладка плитки. Прихожая | |
| 45 | Раскладка плитки. Ванная. Развёртки стен | |
| 46 | Раскладка плитки. Санузел. Развёртки стен | |
| 47 | План полов | |
| 48 | Ведомость отделки помещений | |
| 49 | Колерная карта | |
| 50 | Спецификация отделочных материалов | |
| 51 | Концепция декора и визуализации | |
| 52 | Встроенная мебель. Схема расположения | |
| 53 | Шкаф-купе М9 | |

Общие указания — лист 5: ±0,000 — чистый пол; несущие конструкции и сети дома — по отдельному проекту; скрытые работы — по актам. Открытые вопросы и допущения — листы 6, 7.

| Изм. | Кол.уч | Лист | № док. | Подп. | Дата |
|---|---|---|---|---|---|
| Разраб. | | Кырлан А.С. | | | 04.11.26 |
| Пров. | | | | | |
| ГИП | | | | | |
| | | | | | |
| Н. контр. | | | | | |
| Утв. | | | | | |

**ГД-2026-006-АИ**

Квартира 58 м²

Общая площадь 55,23* м² · * размеры приняты, не замерены (реестр — л. 6, 7, К-5)

Дизайн-проект интерьера

| Стадия | Лист | Листов |
|---|---|---|
| РП | 2 | 87 |

**Общие данные**

М б/м

Кырлан Александр Сергеевич

выпуск 04.11.2026 № 3da8f16a26 · стр. 2 из 96

# Общие данные

Комплект ГД-2026-006-АИ · лист 2 общих данных (продолжение)

**Ведомость рабочих чертежей основного комплекта ГД-2026-006-АИ (продолжение)**

| Лист | Наименование | Примечание |
|---|---|---|
| 54 | Система хранения Г1 | |
| 55 | Кухня (пом. 1). Развёртка гарнитура | |
| 56 | Кухня (пом. 1). Монтажная схема | |
| 57 | Шкафы. Монтажная схема | |
| 58 | Ведомости изделий, техники и фурнитуры | |
| 59 | Реестр марок отделки и позиций альбома | |
| 60 | Схема расположения развёрток и узлов | |
| 61 | Развёртка стены В. Кухня-гостиная (пом. 1), кухонный фронт | |
| 62 | Привязки электроточек и выводов ВК, стена В. Кухня-гостиная (пом. 1) | |
| 63 | Развёртка стены А. Кухня-гостиная (пом. 1) | |
| 64 | Развёртка стены Б. Кухня-гостиная (пом. 1) | |
| 65 | Развёртка стены Г. Кухня-гостиная (пом. 1) | |
| 66 | Развёртка стены А. Спальня (пом. 2) | |
| 67 | Развёртка стены Б. Спальня (пом. 2) | |
| 68 | Привязки электроточек, стена Б. Спальня (пом. 2) | |
| 69 | Развёртка стены В. Спальня (пом. 2) | |
| 70 | Развёртки стен А, Б, В. Ванная (пом. 3) | |
| 71 | Привязки электроточек и выводов ВК, стена В. Ванная (пом. 3) | |
| 72 | Развёртка стены Г. Ванная (пом. 3) | |
| 73 | Развёртки стен А, Б, В. Санузел (пом. 4) | |
| 74 | Развёртка стены Г. Санузел (пом. 4) | |
| 75 | Развёртки стен А, Б. Прихожая (пом. 5) | |
| 76 | Развёртки стен В, Г. Прихожая (пом. 5) | |
| 77 | Привязки электроточек, стена В. Прихожая (пом. 5) | |
| 78 | Развёртки стен А, Б. Гардеробная (пом. 6) | |
| 79 | Развёртка стены Г. Гардеробная (пом. 6) | |
| 80 | Узлы | |
| 81 | Ведомость объёмов работ | |
| 82 | Ведомость объёмов работ (продолжение) | |
| 83 | Ведомость объёмов работ (окончание) | |

**Ведомость рабочих чертежей основного комплекта ГД-2026-006-АИ (продолжение)**

| Лист | Наименование | Примечание |
|---|---|---|
| 84 | Спецификация материалов | |
| 85 | Спецификация материалов (окончание) | |
| 86 | Смета ориентировочная | |
| 87 | Смета ориентировочная (окончание) | |

Общие указания — лист 5: ±0,000 — чистый пол; несущие конструкции и сети дома — по отдельному проекту; скрытые работы — по актам. Открытые вопросы и допущения — листы 6, 7.

**Допущения и предложения на листе**

Основа листа: размеры сняты с плана заказчика, контрольный обмер не выполнен (К-5); высота потолка 2700 мм принята: на плане заказчика не указана (К-5); подрайон климата не задан — принят не северный (жилые от 2,5 м) (К-4); толщины стен приняты: наружные 250 мм, перегородки 120 мм — не обмерены (К-5); разрешённая мощность 15 кВт принята по типовой квартире, технических условий нет (К-6).
См. лист открытых вопросов (лист 6, записи К-4–К-6).

| Изм. | Кол.уч | Лист | № док. | Подп. | Дата | ГД-2026-006-АИ | | |
|---|---|---|---|---|---|---|---|---|
| | | | | | | Квартира 58 м² | | |
| | | | | | | Общая площадь 55,23* м² · * размеры приняты, не замерены (реестр — л. 6, 7, К-5) | | |
| Разраб. | | Кырлан А.С. | | | 04.11.26 | Дизайн-проект интерьера | Стадия: РП | Лист: 3 / Листов: 87 |
| Пров. | | | | | | | | |
| ГИП | | | | | | | | |
| Н. контр. | | | | | | **Общие данные** М б/м | **Кырлан Александр Сергеевич** | |
| Утв. | | | | | | | | |

выпуск 04.11.2026 № 3da8f16a26 · стр. 3 из 96

# Общие данные

Комплект ГД-2026-006-АИ · лист 3 общих данных (продолжение)

## Ведомость ссылочных и прилагаемых документов

| Обозначение | Наименование | Примечание |
|---|---|---|
| | Ссылочные документы | |
| ГОСТ 21.201-2011 | СПДС. Условные графические изображения элементов зданий, сооружений и конструкций | |
| ГОСТ 21.205-2016 | СПДС. Условные обозначения элементов санитарно-технических систем | |
| ГОСТ 21.210-2014 | СПДС. Изображения условные графические электрооборудования и проводок на планах | |
| ГОСТ 2.306-68 | ЕСКД. Обозначения графические материалов и правила их нанесения на чертежах | |
| | Прилагаемые документы | |
| ГД-2026-006-АИ.В1 | Визуализация. Интерьер: Ванная (пом. 3), стена Б | альбом визуализаций |
| ГД-2026-006-АИ.В2 | Визуализация. Интерьер: Ванная (пом. 3), стена В | |
| ГД-2026-006-АИ.В3 | Визуализация. Интерьер: Спальня (пом. 2), стена А | |
| ГД-2026-006-АИ.В4 | Визуализация. Интерьер: Спальня (пом. 2), стена Б | |
| ГД-2026-006-АИ.В5 | Визуализация. Интерьер: Прихожая (пом. 5), стена А | |
| ГД-2026-006-АИ.В6 | Визуализация. Интерьер: Прихожая (пом. 5), стена В | |
| ГД-2026-006-АИ.В7 | Визуализация. Интерьер: Кухня-гостиная (пом. 1), стена Б | |
| ГД-2026-006-АИ.В8 | Визуализация. Интерьер: Кухня-гостиная (пом. 1), стена В | |
| ГД-2026-006-АИ.В9 | Визуализация. Интерьер: Кухня-гостиная (пом. 1), стена Г | |
| ГД-2026-006-АИ.В10 | Визуализация. Интерьер: Гардеробная (пом. 6), общий вид | |
| ГД-2026-006-АИ.В11 | Визуализация. Интерьер: Санузел (пом. 4), общий вид | |

## Состав дизайн-проекта

| Раздел | Состав | Листы |
|---|---|---|
| Обложка | Дизайн-проект интерьера; Квартира 58 м²; автор проекта — Кырлан Александр Сергеевич | 1 с. |
| Концепция | Стиль Скандинавский: концепция интерьера, палитра и материалы (колерная карта лист 49) | л. 17 |
| Визуализации | 11 изобр.: Ванная, стена Б; Ванная, стена В; Спальня, стена А; Спальня, стена Б; Прихожая, стена А; Прихожая, стена В; Кухня-гостиная, стена Б; Кухня-гостиная, стена В; Кухня-гостиная, стена Г; Гардеробная, общий вид; Санузел, общий вид | В1–В11 |
| Рабочие чертежи | планы, развёртки, узлы (развёртки и узлы — листы 34–37, 60, 70, 73, 75, 76, 78, 80) | л. 1–87 |
| Спецификации и ведомости | оборудование, изделия, отделка, электроточки | л. 16, 19, 23, 38, 48–50, 81–85 |

**Допущения и предложения на листе**

Основа листа: размеры сняты с плана заказчика, контрольный обмер не выполнен (К-5); высота потолка 2700 мм принята: на плане заказчика не указана (К-5); подрайон климата не задан — принят не северный (жилые от 2,5 м) (К-4); толщины стен приняты: наружные 250 мм, перегородки 120 мм — не обмерены (К-5); разрешённая мощность 15 кВт принята по типовой квартире, технических условий нет (К-6).
См. лист открытых вопросов (лист 6, записи К-4–К-6).

Общие указания — лист 5: ±0,000 — чистый пол; несущие конструкции и сети дома — по отдельному проекту; скрытые работы — по актам. Открытые вопросы и допущения — листы 6, 7.


| Изм. | Кол.уч | Лист | № док. | Подп. | Дата | ГД-2026-006-АИ | | |
|---|---|---|---|---|---|---|---|---|
| | | | | | | Квартира 58 м² | | |
| | | | | | | Общая площадь 55,23* м² · * размеры приняты, не замерены (реестр — л. 6, 7, К-5) | | |
| Разраб. | | Кырлан А.С. | | | 04.11.26 | Дизайн-проект интерьера | Стадия: РП | Лист: 4 / Листов: 87 |
| Пров. | | | | | | | | |
| ГИП | | | | | | | | |
| Н. контр. | | | | | | Общие данные | Кырлан Александр Сергеевич | |
| Утв. | | | | | | М б/м | | |

выпуск 04.11.2026 № 3da8f16a26 · стр. 4 из 96

# Общие данные

Комплект ГД-2026-006-АИ · лист 4 общих данных (продолжение)

## Условные обозначения

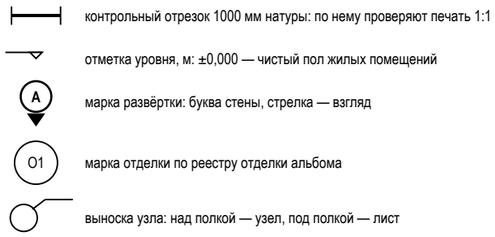


контрольный отрезок 1000 мм натуры: по нему проверяют печать 1:1

отметка уровня, м: ±0,000 — чистый пол жилых помещений

марка развёртки: буква стены, стрелка — взгляд

марка отделки по реестру отделки альбома

выноска узла: над полкой — узел, под полкой — лист

## Общие указания

1. Рабочие чертежи интерьера разработаны на основании задания на проектирование и обмерного плана (лист 14). Объект: Квартира 58 м²; автор проекта — Кырлан Александр Сергеевич; общая площадь 55,23 м², жилая 34,99 м², помещений 6.
2. Рабочие чертежи выполнены в соответствии с заданием на проектирование и нормативными документами, перечисленными в п. 4.
3. Открытые вопросы, принятые допущения и конфликты между разделами, не снятые к выпуску комплекта, сведены в таблицы на листах 6, 7. До ответа по пункту таблицы показанное на указанном там листе — допущение, а не утверждённое решение: комплект по этим листам предварительный.
4. Нормативные документы, на которые есть ссылки в листах комплекта: ГОСТ Р 21.101-2026; ГОСТ 21.501-2018; ГОСТ 2.302-68; ГОСТ 2.303-68; ГОСТ 2.304-81; ГОСТ 2.307-2011; СП 54.13330.2022; СП 71.13330.2017; СП 73.13330.2016; ПУЭ (7-е изд.), гл. 1.8, 7.1; ГОСТ Р 50571.7.701-2024; СанПиН 1.2.3685-21; ГОСТ 2.702; ГОСТ 2.755; ГОСТ 21.110-2013; ГОСТ 21.601; ГОСТ 13996-2019; ГОСТ 23166-2021; ГОСТ 31173-2016; ГОСТ 31565-2012; ГОСТ 32414-2013; ГОСТ 32415-2013; ГОСТ Р 56387-2018; СП 29.13330.2011; СП 30.13330.2020; СП 51.13330.2011; СП 131.13330. Документы из ведомости ссылочных документов здесь не повторяются.
5. За отметку ±0,000 принят уровень чистого пола жилых помещений квартиры (относительная отметка; абсолютная — по проекту дома). Отметка чистого пола мокрых помещений — −0,015. Размеры — в миллиметрах, отметки — в метрах, площади — в м²; высоты установки Н от чистого пола своего помещения до оси изделия.
6. Несущие конструкции, общедомовые стояки, вентиляционные каналы и инженерные сети дома настоящим комплектом не изменяются. Работы, затрагивающие их (проём или штраба в несущей стене, перенос стояка, врезка в вентканал, расширение мокрой зоны), выполняются только по отдельному проекту, к которому прилагается техническое заключение о допустимости и безопасности работ, выданное автором проекта дома или организацией с допуском на обследование, и который согласован в установленном порядке (Жилищный кодекс РФ, ст. 25–29).
7. Трассы инженерных сетей на листах — принципиальные. Расчёты электрических нагрузок и токов КЗ, гидравлики, воздухообмена, освещённости и нагрузок на перекрытие выполняются в проектах ЭОМ, ВК, ОВ и КР организацией с допуском СРО; фактические трассы до закрытия отделкой фиксируются исполнительными схемами.
8. Стиль интерьера — Скандинавский. Палитра проекта: основной — NCS S 1502-Y50R «S 1502-Y50R», NCS S 1002-Y50R «S 1002-Y50R», NCS S 0300-N «S 0300-N»; дополнительный — Tikkurila V503 «Winter»; акцент — NCS S 4010-R90B «S 4010-R90B». Коды цвета — по веерам производителей; цвет утверждается по выкрасу на объекте при освещении проекта.
9. Площади поверхностей — по чистым граням стен до отделки: стены = периметр × высоту от чистого пола помещения до низа потолка минус проёмы (облицовка плиткой — до верха облицовки); плинтус = периметр минус дверные проёмы; пол и потолок — по площади помещения. Количество плиток — по раскладке. Способ один для всех листов комплекта (ведомость отделки, колерная карта, раскладка плитки, развёртки).
10. Марки: стены помещения на всех листах — А (верхняя по плану), Б (правая), В (нижняя), Г (левая); марка отделки О — одна на весь альбом; реестр марок отделки (с позициями колерной карты той же отделки) и марки позиций по видам — на листе 59.
11. Развёртки стен выполнены по всем помещениям для стен с электроточками, мебелью, декором и отделкой: санузлы и кухонный фронт — в М 1:25, остальные стены — в М 1:25; расположение развёрток и узлов — на листе 60, узлы — на листе 80.
12. Перечень скрытых работ, на которые составляются акты освидетельствования (форма по приказу Минстроя России № 344/пр): гидроизоляция пола и стен мокрых помещений (с тестом проливом); стяжка пола (толщина, прочность, влажность основания); тёплый пол до заливки (сопротивление, схема укладки); скрытая электропроводка (за потолком и в штробах стен; условия штробления — в следующем пункте); трубопроводы водоснабжения и канализации до закрытия (опрессовка, уклоны); закладные и усиления под подвесные приборы, мебель и тяжёлый декор, рамы инсталляций; короба дверей скрытого монтажа до штукатурки; каркасы ГКЛ потолков, коробов и перегородок до обшивки.
13. Скрытая электропроводка: за потолком и в штробах стен. Штробы в стенах выполняются только после технического заключения о несущих конструкциях; до заключения несущие стены не определены, и все стены считаются несущими; объём штроб — в ведомости объёмов работ, строка «Штробы в стенах» (вертикальные спуски; объём не меньше фактического, горизонтальные трассы — по исполнительной схеме).
14. Критерии приёмки: допуски отделочных покрытий — по СП 71.13330.2017; испытания систем водоснабжения и канализации — по СП 73.13330.2016 до закрытия трасс; приёмо-сдаточные испытания электроустановки — по ПУЭ, гл. 1.8, с протоколом электролаборатории.
15. Осознанные отступления от ГОСТ Р 21.101-2026, принятые в комплекте: номер листа и число листов («Листов») указаны на каждом листе; на масштабных листах в основной надписи указан фактический масштаб и дан контрольный отрезок 1000 мм; развёртки стен выполнены в М 1:25 (ГОСТ 21.507-81 — 1:50…1:500) ради читаемости привязок; размерные числа и марки элементов (Д-1, ОК-1, О6) кеглем 2,5 мм, номера помещений — в кружке Ø 8 мм (канон — 3,5 мм и Ø 12 мм): так насыщенные листы А3 читаются без наложений надписей.
16. Графы «Пров.», «Н. контр.», «Утв.» основной надписи заполняются при согласовании комплекта с заказчиком; до согласования комплект подписывает автор проекта (графа «Разраб.»).

**Допущения и предложения на листе**

Основа листа: размеры сняты с плана заказчика, контрольный обмер не выполнен (К-5); высота потолка 2700 мм принята: на плане заказчика не указана (К-5); подрайон климата не задан — принят не северный (жилые от 2,5 м) (К-4); толщины стен приняты: наружные 250 мм, перегородки 120 мм — не обмерены (К-5); разрешённая мощность 15 кВт принята по типовой квартире, технических условий нет (К-6).

См. лист открытых вопросов (лист 6, записи К-4–К-6).

| | | | | | | | | |
|---|---|---|---|---|---|---|---|---|
| | | | | | | **ГД-2026-006-АИ** | | |
| | | | | | | Квартира 58 м² | | |
| Изм. | Кол.уч | Лист | № док. | Подп. | Дата | Общая площадь 55,23* м² · * размеры приняты, не замерены (реестр — л. 6, 7, К-5) | | |
| Разраб. | | Кырлан А.С. | | | 04.11.26 | Дизайн-проект интерьера | Стадия | Лист | Листов |
| Пров. | | | | | | | РП | 5 | 87 |
| ГИП | | | | | | | | | |
| | | | | | | **Общие данные** | **Кырлан Александр Сергеевич** | | |
| Н. контр. | | | | | | М б/м | | | |
| Утв. | | | | | | | | | |

выпуск 04.11.2026 № 3da8f16a26 · стр. 5 из 96

# Открытые вопросы, принятые допущения и конфликты. Лист 1 из 2

**ПРЕДВАРИТЕЛЬНО · не для производства работ · открыто пунктов: 10 (реестр — л. 6, 7)**

Сводка по реестрам координации

Комплект предварительный по пунктам этих таблиц. Пока по пункту нет ответа или решения, показанное на указанном листе — допущение проектировщика, а не утверждённое решение.
Сводка: открытых вопросов — 7 (из них ждут факта объекта — 6: контрольного обмера, обследования или документа); изменений в реестре — 3, из них без подписи — 3.
Пункты, ответ на которые лежит на объекте, а не за столом проектировщика (графа «Вид», строка «Ждёт»), собраны на листе «Задание на контрольный обмер и обследование» (листы 8–10): что и где замерить, с какой точностью и чем подтвердить. Пункты, ждущие решения человека, на объекте не закрываются.

## Открытые вопросы и принятые допущения

| № | Формулировка | Вид | Кто решает | Если решения нет | Лист, где это проявляется |
|---|---|---|---|---|---|
| К-1 | Вентканалы на плане заказчика не показаны: ВК-1 принят у перегородки ванной и санузла (со стороны прихожей), ВК-2 — у кухни. От них зависят решётки ВР1–ВР3 и короба. Замерить положение и сечение каналов, проверить тягу. | Отсутствует<br>Ждёт: обмера | Инженер ОВ | решётки ванной и санузла — у ВК-1, кухни — у ВК-2; места — до обмера, лист перевыпустить по факту | л. 27 — План вентиляции |
| К-2 | Ванная (пом. 3), 2140 × 1380 мм в чистоте, проём Д-4 у стены Б. Расстановка проектировщика: ванна 1500 × 700 у стены А от стены Г (была 1600 и заходила в проход перед Д-4 — свободно 240 из 700 мм), умывальник П3 у стены В справа от ванны — перед ним свободно 750 мм (был напротив ванны в 230 мм), полотенцесушитель П5 на стене В между коробом стояков и умывальником. Унитаз П2 из образца раскладки снят: он стоял на стояке Ст К1-1 (короба и люка не поставить), унитаз квартиры — П20 в санузле, инсталляция и короб — там. Остаётся: перед ванной 680 мм до стены В при ориентире 750 мм — это глубина помещения; у умывальника до стены Б 90 мм при ориентире 200 мм. Решить: (а) принять расстановку; (б) душ с поддоном 900 × 900 у стены Г вместо ванны — перед приборами ≥ 750 мм, кадры ванной перерисовать; (в) другой вариант автора. | Спорно<br>Ждёт: решения | Инженер ВК (вода, канализация) | ванна 1500 × 700 и умывальник у стены В по листам; модели ванны и умывальника не заказывать до решения | л. 29 — План выводов сантехники<br>л. 18 — План расстановки мебели |
| К-3 | Скрытые двери Д-2, Д-3, Д-4 стоят в существующих проёмах прихожей, размеров в свету нет: короб скрытой двери шире и выше полотна на 100–120 / 50–80 мм, полотно по проёму 2100 под ряд 2000 не встаёт (по каталогам нужно 2050–2080). У Д-3 (спальня) и Д-4 (санузел) откос от угла 40 мм — под короб нужно не меньше 50. Замерить проёмы в чистоте и откосы; решить: проёмы подрезать/расширить на 10+ мм от угла (если стена не несущая) или взять модель с узким коробом; высоту проёма — по выбранной модели. | Отсутствует<br>Ждёт: обмера, затем решения | Архитектор-планировщик | блоки скрытых дверей не заказывать до замера; полотна на листах — расчётные («расч.»), проёмы не переносятся | л. 16 — План дверей и ведомость заполнения проёмов |
| К-4 | Климатический подрайон (СП 131.13330) не задан: принят не северный — жилые комнаты и кухня под потолком от 2,5 м (СП 54, п. 5.12); в IA, IБ, IГ, IД, IVA — от 2,7 м. | Отсутствует<br>Ждёт: документа | Архитектор-планировщик | отметки потолков жилых — по 2,5 м; при северном подрайоне уровни ниже 2,7 м пересчитать до заказа каркаса | л. 40 — План потолков |
| К-5 | Основа альбома — план заказчика без контрольного обмера: размеры помещений сняты с плана, высота потолка 2700 мм и толщины стен (наружные 250 мм, перегородки 120 мм) приняты — на плане они не указаны. От них зависят вертикальные размеры (развёртки, шкафы, плитка, потолки), объёмы работ и сборка шкафов-купе. Выполнить контрольный обмер. | Непонятно<br>Ждёт: обмера | Архитектор-планировщик | размеры, высота потолка и толщины стен — принятые; мебель на заказ, двери и каркас потолков не заказывать до обмера | л. 14 — Обмерный план |
| К-6 | Разрешённая мощность 15 кВт принята по типовой квартире, технических условий в материалах объекта нет. Сверить с техническими условиями. | Непонятно<br>Ждёт: документа | Инженер-электрик | вводной аппарат и группы щита — по 15 кВт; при меньшей мощности схему щита пересчитать до монтажа | л. 24 — Однолинейная схема щита |
| К-7 | Места стиральной машины в квартире не было. В ванной 2,2 × 1,5 м и санузле места 600 × 600 с подходом нет. Предложение исполнителя: узкая машина 600 × 450 под столешницей кухни вместо модуля с ящиками М11 справа от варочной, ряд удлиняется на 220 мм; отдельная группа щита с УЗО 30 мА. Решить: принять, или машина в ванной вместо ванны (душ), или отказ от машины (прачечная) решением автора | Предложение<br>Ждёт: документа, затем решения | Инженер ВК (вода, канализация) | стиральная машина П6 в кухне под столешницей (ниша вместо М11, 2800…3420) — как на листах | л. 29 — План выводов сантехники<br>л. 18 — План расстановки мебели<br>л. 24 — Однолинейная схема щита |

| Изм. | Кол.уч | Лист | № док. | Подп. | Дата |
|---|---|---|---|---|---|
| Разраб. | | Кырлан А.С. | | | 04.11.26 |
| Пров. | | | | | |
| ГИП | | | | | |
| | | | | | |
| Н. контр. | | | | | |
| Утв. | | | | | |

**ГД-2026-006-АИ**

Квартира 58 м²

Общая площадь 55,23* м² · * размеры приняты, не замерены (реестр — л. 6, 7, К-5)

Дизайн-проект интерьера

| Стадия | Лист | Листов |
|---|---|---|
| РП | 6 | 87 |

**Открытые вопросы, принятые допущения и конфликты. Лист 1 из 2**
М б/м

**Кырлан Александр Сергеевич**

выпуск 04.11.2026 № 3da8f16a26 · стр. 6 из 96

# Открытые вопросы, принятые допущения и конфликты. Лист 2 из 2

ПРЕДВАРИТЕЛЬНО · не для производства работ · открыто пунктов: 10 (реестр — л. 6, 7)

Сводка по реестрам координации

### Изменения проекта после выпуска листов (реестр изменений)

| № | Дата | Лист | Было | Стало | Кто решил, подпись |
|---|---|---|---|---|---|
| ИЗ-1 | 30.10.2026 | л. 20 — План розеток и электровыводов<br>л. 22 — План выключателей и схема включения<br>л. 21 — План освещения<br>л. 58 — Ведомости изделий, техники и фурнитуры | Кухня-гостиная: ТВ1, LAN1 и розетка «ТВ, приставка» стояли на стене В (привязка 3300…3450, кухонная стена), а ТВ-тумба М20 — на стене Г (1500…3300): за телевизором точек не было. Выключатель S1 — на стене Г в зоне экрана, у двери Д-2 выключателя не было. Светильник гардеробной Св16 — на линии L6 подсветки кухонной столешницы, выключателя в гардеробной нет. Ванная и санузел — одна линия L4 с одним выключателем S4. Вытяжка в М10 без вывода питания; розетка холодильника без привязки к модулю М4. | ТВ1 (2400), LAN1 (2550) и розетка приставки (2400, H=300) — на стене Г по оси тумбы М20. S1 стена В, привязка 4950 (150 мм от проёма Д-2 со стороны ручки), S5 у дивана — проходной. Св16 — линия L7, выключатель S8 на стене Г гардеробной у Д-3 (привязка 1500). Санузел — линия L9, выключатель S9 в прихожей у Д-4 санузла (стена Г, привязка 1450); S4 — только ванная (L4, вентилятор ВР2). Розетка вытяжки — стена В привязка 2500, H=2200, группа 2 (для М10); розетка холодильника — для М4. | Не утверждено: подписи нет. решение исполнителя; на утверждение А. С. Кырлана |
| ИЗ-2 | 30.10.2026 | л. 18 — План расстановки мебели<br>л. 19 — Спецификация мебели и оборудования | Диван М1 на стене Б привязка 1300…3500: торец в 500 мм от стены В, дверь Д-2 (3900…4800) открывалась в торец дивана. Кресло М22 х 4250, у 450. | Диван М1 привязка 1000…3200 — перед проёмом 800 мм; кресло М22 х 3500…4300, у 450 у окна 2. Выключатель S5 и розетка у дивана — привязка 900. Знак «**» у М1, М22 до подписи автора. | Не утверждено: подписи нет. решение исполнителя; предложение проектировщика, на утверждение А. С. Кырлана |
| ИЗ-3 | 30.10.2026 | л. 27 — План вентиляции | Внутренний блок КВ-1 на стене А привязка 3300…4200 — внутри оконного проёма 3200…4800; наружный КН-1 привязка 3350 — на окне. | КВ-1 — стена Г, привязка 300…1200 (простенок у окна 1), КН-1 — стена А, простенок между окнами 2400…3200. Трасса ≈ 3 м (петля принята по минимуму, паспорта модели нет). Знак «**» у КВ-1 до подписи автора. | Не утверждено: подписи нет. решение исполнителя; предложение проектировщика, на утверждение А. С. Кырлана |

### Примечания

1. Номера листов — по ведомости рабочих чертежей комплекта (лист «Общие данные»).
2. Графа «Если решения нет» показывает состояние решения на листах; влияние на сроки и стоимость по пунктам не оценивалось.
3. Пункт, по которому принято решение, при следующем выпуске комплекта из таблиц исключается.

| Изм. | Кол.уч | Лист | № док. | Подп. | Дата | ГД-2026-006-АИ | | |
|---|---|---|---|---|---|---|---|---|
| | | | | | | Квартира 58 м² | | |
| | | | | | | Общая площадь 55,23* м² · * размеры приняты, не замерены (реестр — л. 6, 7, К-5) | | |
| Разраб. | | Кырлан А.С. | | | 04.11.26 | Дизайн-проект интерьера | Стадия: РП | Лист: 7 / Листов: 87 |
| Пров. | | | | | | | | |
| ГИП | | | | | | | | |
| Н. контр. | | | | | | **Открытые вопросы, принятые допущения и конфликты. Лист 2 из 2**<br>М б/м | **Кырлан Александр Сергеевич** | |
| Утв. | | | | | | | | |

выпуск 04.11.2026 № 3da8f16a26 · стр. 7 из 96

# Задание на контрольный обмер и обследование. Лист 1 из 3

**ПРЕДВАРИТЕЛЬНО · не для производства работ · открыто пунктов: 10 (реестр — л. 6, 7)**

Что замерить, вскрыть и получить до заказа материалов и изделий

Задание собрано из открытых вопросов, ответ на которые лежит на объекте или в документах, а не за столом проектировщика. Пока факт не получен, размер, материал или положение на листах — допущение (знак «*»), а не замер.
Сводка: на объекте — 9 (до демонтажа — 7; после демонтажа — 2); документом и при закупке — 4; из допущений в данных и на листах — 9, из них без вопроса в реестре — 6. Закрываются вопросы: К-1, К-3–К-7 (6). Вопросы, ждущие решения человека, задание не закрывает — они решаются по реестру открытых вопросов.

## Условия проведения

| Порядок работ | Приёмы и точность | Кто присутствует | Если факт не совпал с проектом |
|---|---|---|---|
| 1. До демонтажа — существующее состояние: контур, диагонали, высоты, проёмы, оси стояков, ниши и конструкции, которые видны.<br>2. После демонтажа, до черновых работ — то, что закрывали отделка и короба: основание стен, фактические толщины, углы, узлы.<br>3. Документы и данные закупки — не на объекте: к сроку из последней таблицы, от них зависят привязки и заказ.<br>Что заказывается по размеру из задания, до закрытия пункта не заказывают: сроки изготовления — по графику закупок прораба. | Обход по часовой стрелке от входа: стены, проёмы, потолок, коммуникации (стояки, щиток, вентканалы), особенности (ниши, короба, выступы).<br>Размеры записывают в мм; сумма участков равна общему размеру, при цепочке длиннее трёх участков ставят проверочный (общий) размер.<br>Диагонали каждого помещения; если две диагонали различаются на 5 мм и больше, разницу подписывают на плане.<br>Потолок — в нескольких точках: центр, углы, у проёмов. Проём — ширина, высота, глубина откоса, привязка к ближайшим углам, высота подоконника.<br>Допустимая погрешность прибора — 2–3 мм на метр; размеры округляют кратно 5 мм; два контрольных промера одного размера не должны расходиться более чем на 2 %. Допуск по пункту — в графе «Точность».<br>План БТИ обмер не заменяет. | Прораб (отвечает за проведение) — назначает день и порядок обхода, открывает объект и освобождает помещения, ведёт это задание и реестр изменений.<br>Архитектор — выполняет обмер, составляет акт контрольного обмера и подписывает результаты по размерам и конструкциям.<br>Владельцы вопросов присутствуют при пунктах своего раздела или принимают результат до заказа: Инженер ОВ — К-1; позиции О-13, О-3; Инженер-электрик — К-6; позиции О-2; Инженер ВК (вода, канализация) К-7; позиции О-1; Отделочник — позиции О-8, О-9.<br>Заказчик или его представитель — передаёт документы (план БТИ, проект дома, технические условия, паспорта), подписывает акт. Проектных решений на обмере не принимают: обмер даёт факт, решения — по реестру открытых вопросов (листы 6–7). | 1. В пределах допуска пункта — принимается измеренное значение, лист перевыпускается, знак «*» снимается.<br>2. Больше допуска или контрольные промеры расходятся более чем на 2 % — промер повторяют; не подтвердилось — запись в реестр изменений (дата, лист, было, стало, кто решил, подпись), работы в этом месте не начинают.<br>3. Затронуты несущая стена, стояк, вентканал или мокрая зона — сразу владельцу раздела и ГИПу (главному инженеру проекта); между разделами не больше двух кругов, затем решает ГИП.<br>4. На объекте устно ничего не согласуется: каждое решение — записью в реестр с подписью. |

## Этап 1. До демонтажа

| № | Где | Способ | Что сделать | Кто выполняет | Точность | Что пересчитается в альбоме | Чем подтверждается | Закрывает вопросы реестра |
|---|---|---|---|---|---|---|---|---|
| О-1 | Ввод В1 и Т3 у стояков; по всей квартире | Обмер | Отключающая арматура и счётчики воды на вводах: положение, тип, пломбы управляющей компании. Альбом ставит их на каждом вводе по практике, в данных их нет. | Архитектор | ±5 мм | Узлы ввода в спецификации ВК (краны, фильтры, счётчики); места ввода на плане выводов.<br>Листы:<br>л. 29 — План выводов сантехники<br>л. 38 — Спецификация сантехнического оборудования | акт контрольного обмера; фото с рулеткой и привязкой к стене или углу | Вопроса в реестре нет: Альбом принимает счётчики воды на вводах без осмотра.<br>Результат принимает: Инженер ВК (вода, канализация) |
| О-2 | Вход в квартиру или лестничная клетка; место щита на плане | Обмер | Существующий щиток и счётчик электроэнергии: место и габарит ниши, состояние ввода, марка и сечение вводного кабеля, наличие вводного автомата и УЗО, пломбы. | Архитектор | ±5 мм | Ниша и место щита на листах; вводной кабель и аппараты на однолинейной схеме; расстояния до первых групп.<br>Листы:<br>л. 24 — Однолинейная схема щита | акт контрольного обмера; фото с рулеткой и привязкой к стене или углу | Вопроса в реестре нет: Альбом принимает щит и ввод без осмотра.<br>Результат принимает: Инженер-электрик |
| О-3 | у окон | Обмер | Положение стояков отопления (подающий и обратный) от граней стен, диаметры, наличие запорной арматуры; существующие радиаторы: число секций, межосевое расстояние, подводки. В данных стояков отопления нет — лист отопления выводит их условно у откоса окна. | Архитектор | ±5 мм | План отопления: места стояков и подводок, привязки радиаторов; подбор радиаторов по теплотехническому расчёту; радиаторы и узлы подключения в ВОР и спецификации.<br>Листы:<br>л. 28 — План отопления | акт контрольного обмера; фото с рулеткой и привязкой к стене или углу | Вопроса в реестре нет: Альбом принимает положение стояков и радиаторов отопления без обмера.<br>Результат принимает: Инженер ОВ |
| О-4 | санузел, ванная, кухня | Обмер | Положение и сечение вентканалов (вентблока), тяга. | исполнитель | ±10 мм | план вентиляции, потолки, короба<br>Листы:<br>л. 27 — План вентиляции | акт контрольного обмера | К-1<br>Результат принимает: Инженер ОВ |
| О-5 | прихожая (пом. 5) | Обмер | Проёмы Д-2, Д-3, Д-4 в чистоте (ширина, высота от чистого пола) и откосы до углов прихожей. | исполнитель | ±5 мм | ведомость заполнения проёмов, план дверей<br>Листы:<br>л. 16 — План дверей и ведомость заполнения проёмов | акт контрольного обмера | К-3<br>Результат принимает: Архитектор |

**Допущения и предложения на листе**
Основа листа: размеры сняты с плана заказчика, контрольный обмер не выполнен (К-5); высота потолка 2700 мм принята: на плане заказчика не указана (К-5); подрайон климата не задан — принят не северный (жилые от 2,5 м) (К-4); толщины стен приняты: наружные 250 мм, перегородки 120 мм — не обмерены (К-5); разрешённая мощность 15 кВт принята по типовой квартире, технических условий нет (К-6).
См. лист открытых вопросов (лист 6, записи К-4–К-6).

| Изм. | Кол.уч | Лист | № док. | Подп. | Дата |
|---|---|---|---|---|---|
| Разраб. | | Кырлан А.С. | | | 04.11.26 |
| Пров. | | | | | |
| ГИП | | | | | |
| | | | | | |
| Н. контр. | | | | | |
| Утв. | | | | | |

**ГД-2026-006-АИ**

Квартира 58 м²

Общая площадь 55,23* м² · * размеры приняты, не замерены (реестр — л. 6, 7, К-5)

Дизайн-проект интерьера

| Стадия | Лист | Листов |
|---|---|---|
| РП | 8 | 87 |

**Задание на контрольный обмер и обследование.**
**Лист 1 из 3**
М б/м

**Кырлан Александр Сергеевич**

выпуск 04.11.2026 № 3da8f16a26 · стр. 8 из 96

# Задание на контрольный обмер и обследование. Лист 2 из 3

ПРЕДВАРИТЕЛЬНО · не для производства работ · открыто пунктов: 10 (реестр — л. 6, 7)

Что замерить, вскрыть и получить до заказа материалов и изделий

### Этап 1. До демонтажа (продолжение)

| № | Где | Способ | Что сделать | Кто выполняет | Точность | Что пересчитается в альбоме | Чем подтверждается | Закрывает вопросы реестра |
|---|---|---|---|---|---|---|---|---|
| О-6 | По месту | Обмер | Подтвердить на объекте принятое: подрайон климата не задан — принят не северный (жилые от 2,5 м) | Архитектор | ±5 мм | Листы, где используется принятая величина.<br>Листы:<br>л. 2–5 — Общие данные | акт контрольного обмера | К-4<br>Результат принимает: Архитектор |
| О-7 | все помещения квартиры | Обмер | Контрольный обмер всех помещений: стороны, диагонали, проёмы, толщины стен; высота потолка в каждом помещении в нескольких точках (центр, углы, у проёмов). Принято: потолок 2700 мм, стены 250 / 120 мм. | исполнитель | ±5 мм | обмерный и монтажный планы, развёртки, план потолков, шкафы, объёмы работ<br>Листы:<br>л. 14 — Обмерный план | акт контрольного обмера | К-5<br>Результат принимает: Архитектор |

### Этап 2. После демонтажа, до черновых работ

| № | Где | Способ | Что сделать | Кто выполняет | Точность | Что пересчитается в альбоме | Чем подтверждается | Закрывает вопросы реестра |
|---|---|---|---|---|---|---|---|---|
| О-8 | Кухня-гостиная (пом. 1), Спальня (пом. 2), Ванная (пом. 3), Санузел (пом. 4), Прихожая (пом. 5), Гардеробная (пом. 6) | Обмер | Нивелировка плиты перекрытия и существующего пола после демонтажа покрытий: отметки в углах и по сетке, перепады по помещению, уклоны, отметки порогов (чистый пол в мокрых зонах принят -15 мм, 0 мм). Принятая толщина стяжки 33 мм, 50 мм и отметка чистого пола — расчётные, не от замера плиты. | Архитектор | ±5 мм по отметке; ровность просвет под 2-метровой рейкой, горизонталь против 0,2 % длины помещения | Толщина стяжки и отметка чистого пола; уклоны к трапам и пороги; выпуски К1 относительно чистого пола (план разводки); объёмы стяжки и смеси в ВОР и спецификации.<br>Листы:<br>л. 43, 47 — План полов<br>л. 30 — Схема разводки водопровода и канализации | акт контрольного обмера | Вопроса в реестре нет: Альбом принимает отметки плиты и толщину пирога пола без нивелировки.<br>Результат принимает: Отделочник |
| О-9 | Кухня-гостиная (пом. 1), Спальня (пом. 2), Ванная (пом. 3), Санузел (пом. 4), Прихожая (пом. 5), Гардеробная (пом. 6) | Обмер | Вертикаль и плоскостность стен: отклонение от вертикали по высоте стены (отвес или лазерный уровень), просвет под правилом 2 м, кривизна углов. Нужно там, где от стены зависит изделие: облицовка плиткой (пом. 3, 4), штукатурка и окраска (пом. 1, 2, 5, 6), встроенная мебель и кухня (пом. 1, 5). | Архитектор | до 1 мм на 2 м (правило и клиновой щуп); вертикаль — мм на высоту стены, отклонения подписываются на плане | Толщина штукатурки и расход смеси в ВОР и спецификации; раскладка плитки (подрезка у стен); зазоры и крепление встроенной мебели и кухни.<br>Листы:<br>л. 43–46 — Раскладка плитки<br>л. 48 — Ведомость отделки помещений | акт контрольного обмера | Вопроса в реестре нет: Альбом принимает стены ровными и вертикальными без замера.<br>Результат принимает: Отделочник |

### Документы и данные закупки (не на объекте)

| № | У кого, откуда | Способ | Что получить | К какому сроку | Что пересчитается в альбоме | Чем подтверждается | Закрывает вопросы реестра |
|---|---|---|---|---|---|---|---|
| О-10 | адрес объекта, СП 131.13330 | Документ | Климатический подрайон по СП 131.13330 (по адресу объекта) | до заказа каркаса потолков | план потолков, разрезы, ведомость объёмов<br>Листы:<br>л. 40 — План потолков | копия документа | К-4<br>Результат принимает: Архитектор |
| О-11 | заказчик; организация, выдавшая технические условия | Документ | Технические условия на присоединение: разрешённая мощность (принято 15 кВт по типовой квартире). | до утверждения однолинейной схемы щита | однолинейная схема щита: вводной аппарат и группы<br>Листы:<br>л. 24 — Однолинейная схема щита | копия документа | К-6<br>Результат принимает: Инженер-электрик |

**Допущения и предложения на листе**

Основа листа: размеры сняты с плана заказчика, контрольный обмер не выполнен (К-5); высота потолка 2700 мм принята: на плане заказчика не указана (К-5); подрайон климата не задан — принят не северный (жилые от 2,5 м) (К-4); толщины стен приняты: наружные 250 мм, перегородки 120 мм — не обмерены (К-5); разрешённая мощность 15 кВт принята по типовой квартире, технических условий нет (К-6).

См. лист открытых вопросов (лист 6, записи К-4–К-6).

| Изм. | Кол.уч | Лист | № док. | Подп. | Дата |
|---|---|---|---|---|---|
| Разраб. | | Кырлан А.С. | | | 04.11.26 |
| Пров. | | | | | |
| ГИП | | | | | |
| | | | | | |
| Н. контр. | | | | | |
| Утв. | | | | | |

**ГД-2026-006-АИ**

Квартира 58 м²

Общая площадь 55,23* м² · * размеры приняты, не замерены (реестр — л. 6, 7, К-5)

| Дизайн-проект интерьера | Стадия | Лист | Листов |
|---|---|---|---|
| | РП | 9 | 87 |

**Задание на контрольный обмер и обследование.**
**Лист 2 из 3**
М б/м

**Кырлан Александр Сергеевич**

выпуск 04.11.2026 № 3da8f16a26 · стр. 9 из 96

# Задание на контрольный обмер и обследование. Лист 3 из 3

**ПРЕДВАРИТЕЛЬНО · не для производства работ · открыто пунктов: 10 (реестр — л. 6, 7)**

Что замерить, вскрыть и получить до заказа материалов и изделий

## Документы и данные закупки (не на объекте) (продолжение)

| № | У кого, откуда | Способ | Что получить | К какому сроку | Что пересчитается в альбоме | Чем подтверждается | Закрывает вопросы реестра |
|---|---|---|---|---|---|---|---|
| О-12 | паспорт модели | Документ | Модель стиральной машины: габарит (ширина 600, глубина ≤ 450, высота ≤ 850 под столешницу), тип загрузки, положение подвода и слива | до заказа кухни | ниша М11** кухни, выводы В1/К1, розетка<br>Листы:<br>л. 29 — План выводов сантехники<br>л. 18 — План расстановки мебели<br>л. 24 — Однолинейная схема щита | копия документа | К-7<br>Результат принимает: Инженер ВК (вода, канализация) |
| О-13 | Поставщик изделий; Спальня (пом. 2) | Закупка | Паспорт или монтажная схема выбранной модели: КВ-2* допустимая длина трассы фреона (минимальная и максимальная), перепад высот между блоками, место наружного блока. Принято в проекте: длина петли принята по типовому минимуму 3 м; паспорта выбранной модели нет. | До закрытия трасс и разводки | Габариты и положение изделий на планах и развёртках, выводы (вода, слив, электро), монтажные зазоры; знак «*» у марки снимается паспортом или чертежом.<br>Листы:<br>л. 18 — План расстановки мебели | паспорт изделия или партии | Вопроса в реестре нет<br>Результат принимает: Инженер ОВ |

## Примечания

1. Подтверждение: акт контрольного обмера (дата, кто присутствовал, прибор, перечень промеров с результатами, подписи присутствующих); к акту — фото вскрытий и узлов и техническое заключение организации, выполнившей обследование.
2. Номера листов — по ведомости рабочих чертежей комплекта (лист «Общие данные»).
3. Пункт исключается из задания при следующем выпуске, когда акт подписан, значение внесено в проект и листы перевыпущены; знак «*» у величины снимается только замером.

**Допущения и предложения на листе**

Основа листа: размеры сняты с плана заказчика, контрольный обмер не выполнен (К-5); высота потолка 2700 мм принята: на плане заказчика не указана (К-5); подрайон климата не задан — принят не северный (жилые от 2,5 м) (К-4); толщины стен приняты: наружные 250 мм, перегородки 120 мм — не обмерены (К-5); разрешённая мощность 15 кВт принята по типовой квартире, технических условий нет (К-6).

Знак «*» — принято, не замерено и не подтверждено (замерить на объекте): КВ-2 — длина петли принята по типовому минимуму 3 м; паспорта выбранной модели нет.

Знак «**» — предложение проектировщика, заказчиком не утверждено (согласовать с заказчиком): К-7: М11 — место стиральной машины: вместо модуля с ящиками 400 справа от варочной; ряд до 3420, журнальный стол М21 (с х 3440) не мешает загрузке.

См. лист открытых вопросов (лист 6, записи К-4–К-7).

| Изм. | Кол.уч | Лист | № док. | Подп. | Дата |
|---|---|---|---|---|---|
| Разраб. | | Кырлан А.С. | | | 04.11.26 |
| Пров. | | | | | |
| ГИП | | | | | |
| | | | | | |
| Н. контр. | | | | | |
| Утв. | | | | | |

**ГД-2026-006-АИ**

Квартира 58 м²

Общая площадь 55,23* м² · * размеры приняты, не замерены (реестр — л. 6, 7, К-5)

Дизайн-проект интерьера

| Стадия | Лист | Листов |
|---|---|---|
| РП | 10 | 87 |

**Задание на контрольный обмер и обследование.**
**Лист 3 из 3**
М б/м

**Кырлан Александр Сергеевич**

выпуск 04.11.2026 № 3da8f16a26 · стр. 10 из 96

# График закупок и работ. Лист 1 из 3

**ПРЕДВАРИТЕЛЬНО · не для производства работ · открыто пунктов: 10 (реестр — л. 6, 7)**

Что заказывать и когда не раньше чего: относительный порядок без дат; срок поставки — из данных или «не задан» с записью реестра

Лист не содержит дат: контрольного обмера, подписанных решений автора и договоров ещё нет, и любая дата была бы выдумана. Вместо календаря — порядок и условия: замер → решение и выбор изделия → заказ → срок поставки → работа, которую позиция блокирует.
Срок поставки печатается как срок, только если он задан в данных позиции. Нет — «срок поставки не задан» и ссылка на вопрос реестра о сроках; типовой диапазон практики стоит рядом как ориентир и заказывать по нему нельзя. Номера З-N и Р-N — строки этого листа, К-N — записи реестра открытых вопросов, О-N — позиции задания на контрольный обмер.

## Закупки: что заказывается, от чего зависит заказ и какую работу блокирует

| № | Позиция и где | 1. Замер до заказа | 2. Решение, выбор изделия, паспорт | 3. Условие заказа | 4. Срок поставки | 5. Блокирует работу | Закрывает вопросы реестра |
|---|---|---|---|---|---|---|---|
| З-1 | Двери скрытого монтажа с коробом под покраску в существующих проёмах: Д-2, Д-3, Д-4 — 5 шт.<br>пом. 5, 6 | О-7: обмер: все помещения квартиры (К-5); до заказа мебели, дверей и каркаса потолков | | После 1 и 2 и после получения срока у поставщика (вопроса о сроках нет); дата заказа — когда срок известен, не позднее чем за срок до начала Р-5. | срок поставки не задан (записи реестра нет)<br>Ориентир практики (не срок поставщика): ≈ 30 дн. | Р-5 «штукатурка»: короб ставят до штукатурки (коробку ставят на черновой стадии; полотно навешивают после чистовой отделки стен) | К-5 |
| З-2 | Кухонный гарнитур по проекту кухни: модули М4, М5, М6, М7, М11**, М8, М10<br>пом. 1 | | | После 1 и 2 и после получения срока у поставщика (вопроса о сроках нет); дата заказа — когда срок известен, не позднее чем за срок до начала Р-15. | срок поставки не задан (записи реестра нет)<br>Ориентир практики (не срок поставщика): 4–8 нед. от замера | Р-15 «кухня и мебель»: замер кухни — по готовым стенам после штукатурки или плитки, до чистового пола; производство идёт параллельно со стяжкой и отделкой | |
| З-3 | Встраиваемая техника кухни: М4 холодильник, М11** washer<br>пом. 1 | | | После 1 и 2 и после получения срока у поставщика (вопроса о сроках нет); дата заказа — когда срок известен, не позднее чем за срок до начала Р-15. | срок поставки не задан (записи реестра нет) | Р-15 «кухня и мебель»: паспорта и монтажные схемы — до изготовления модулей кухни: нишу и вентзазоры задаёт модель, а не типовая схема 60 см | |
| З-4 | Стиральная машина: П6** (вертикальная загрузка 400 × 600 мм — условие закупки)<br>пом. 1 | | О-12: Модель стиральной машины: габарит (ширина 600, глубина ≤ 450, высота ≤ 850 под столешницу), тип загрузки, положение подвода и слива (К-7); до заказа кухни | После 1 и 2 и после получения срока у поставщика (вопроса о сроках нет); дата заказа — когда срок известен, не позднее чем за срок до начала Р-4. | срок поставки не задан (записи реестра нет) | Р-4 «черновая сантехника»: габарит и подводка — до закрытия люка и разводки | К-7 |
| З-5 | Сантехнические приборы и инсталляции: П4, П1**, П3**, П20<br>пом. 1, 3, 4 | О-3: обмер: у окон | | После 1 и 2 и после получения срока у поставщика (вопроса о сроках нет); дата заказа — когда срок известен, не позднее чем за срок до начала Р-4. | срок поставки не задан (записи реестра нет) | Р-4 «черновая сантехника»: инсталляцию ставят до обшивки ГКЛВ и до гидроизоляции стены | |
| З-6 | Керамогранит и плитка: 2 поз. по артикулу и формату, 46,11 м² по раскладке<br>пом. 3, 4, 5 | О-8: обмер: Кухня-гостиная (пом. 1), Спальня (пом. 2), Ванная (пом. 3), Санузел (пом. 4), Прихожая (пом. 5), Гардеробная (пом. 6)<br>О-9: обмер: Кухня-гостиная (пом. 1), Спальня (пом. 2), Ванная (пом. 3), Санузел (пом. 4), Прихожая (пом. 5), Гардеробная (пом. 6) | | После 1 и 2 и после получения срока у поставщика (вопроса о сроках нет); дата заказа — когда срок известен, не позднее чем за срок до начала Р-9. | срок поставки не задан (записи реестра нет) | Р-9 «плитка»: калибр партии измеряют до раскладки, раскладку пересчитывают до заказа | |
| З-7 | Покрытие пола (доска) и плинтус: пом. 1, 2, 6<br>пом. 1, 2, 6 | О-8: обмер: Кухня-гостиная (пом. 1), Спальня (пом. 2), Ванная (пом. 3), Санузел (пом. 4), Прихожая (пом. 5), Гардеробная (пом. 6) | | После 1 и 2 и после получения срока у поставщика (вопроса о сроках нет); дата заказа — когда срок известен, не позднее чем за срок до начала Р-12. | срок поставки не задан (записи реестра нет) | Р-12 «чистовые полы»: артикул и партия — до заказа; доску привозят к чистовым полам | |
| З-8 | Встроенная мебель по замеру цеха: М9<br>пом. 5 | О-7: обмер: все помещения квартиры (К-5); до заказа мебели, дверей и каркаса потолков | | После 1 и 2 и после получения срока у поставщика (вопроса о сроках нет); дата заказа — когда срок известен, не позднее чем за срок до начала Р-15. | срок поставки не задан (записи реестра нет)<br>Ориентир практики (не срок поставщика): 4–8 нед. от замера | Р-15 «кухня и мебель»: цех замеряет по готовым стенам; производство 4–8 недель идёт параллельно с отделкой | К-5 |

**Допущения и предложения на листе**

Основа листа: размеры сняты с плана заказчика, контрольный обмер не выполнен (К-5); высота потолка 2700 мм принята: на плане заказчика не указана (К-5); подрайон климата не задан — принят не северный (жилые от 2,5 м) (К-4); толщины стен приняты: наружные 250 мм, перегородки 120 мм — не обмерены (К-5); разрешённая мощность 15 кВт принята по типовой квартире, технических условий нет (К-6).

Знак «**» — предложение проектировщика, заказчиком не утверждено (согласовать с заказчиком): К-2: П1 — ванна 1500 вместо 1600 — не заходит в проход перед проёмом Д-4; перед ванной 680 мм — глубина помещения; П3 — умывальник у стены В справа от ванны — перед ним свободно 750 мм, до стены Б 90 мм; К-7: М11 — место стиральной машины: вместо модуля с ящиками 400 справа от варочной; ряд до 3420, журнальный стол М21 (с х 3440) не мешает загрузке; П6 — стиральная машина на кухне: в ванной и санузле места нет; подвод ХВС с шаровым краном, слив — встраиваемый сифон с обратным клапаном (водяной затвор), отдельная группа 6 щита с УЗО 30 мА.

См. лист открытых вопросов (лист 6, записи К-2, К-4–К-7).

| Изм. | Кол.уч | Лист | № док. | Подп. | Дата |
|---|---|---|---|---|---|
| Разраб. | | Кырлан А.С. | | | 04.11.26 |
| Пров. | | | | | |
| ГИП | | | | | |
| | | | | | |
| Н. контр. | | | | | |
| Утв. | | | | | |

**ГД-2026-006-АИ**

Квартира 58 м²

Общая площадь 55,23* м² · * размеры приняты, не замерены (реестр — л. 6, 7, К-5)

Дизайн-проект интерьера

| Стадия | Лист | Листов |
|---|---|---|
| РП | 11 | 87 |

**График закупок и работ. Лист 1 из 3**

М б/м

**Кырлан Александр Сергеевич**

выпуск 04.11.2026 № 3da8f16a26 · стр. 11 из 96

# График закупок и работ. Лист 2 из 3

ПРЕДВАРИТЕЛЬНО · не для производства работ · открыто пунктов: 10 (реестр — л. 6, 7)

Что заказывать и когда не раньше чего: относительный порядок без дат; срок поставки — из данных или «не задан» с записью реестра

## Работы: порядок и что не даёт начать

| № | Работа (стадия технологической последовательности) | После | Что должно быть к началу: условия и закупки | Не начинать, пока открыто в реестре |
|---|---|---|---|---|
| Р-1 | Демонтаж покрытий, отделки стен и потолков, дверных блоков и приборов; конструкции, стены и перегородки не трогать до технического заключения (стадия 1) | | до начала: запрошены документы на дом и БТИ; контрольный обмер до демонтажа (что видно) сделан | |
| Р-2 | Контрольный обмер на голых стенах и обследование (задание — лист «Задание на контрольный обмер») (стадия 2) | Р-1 | после снятия отделки: видны стояки, каналы, щиток, толщины стен; до заказа всего, что делают по размеру | |
| Р-3 | Черновая электрика: штробы, короба, гофра, подрозетники, щит (стадия 4) | Р-2 | до начала: план электрики с высотами утверждён; штробы в стенах — только после технического заключения; мебель расставлена | К-6: Разрешённая мощность 15 кВт принята по типовой квартире, технических условий в материалах объекта нет. |
| Р-4 | Черновая сантехника и вентиляция: разводка, выводы, инсталляции, короба стояков (стадия 5) | Р-2 | до начала: положение стояков замерено; модели инсталляций и машины выбраны (габариты рамы, подводка); инсталляцию ставят до обшивки ГКЛВ и до гидроизоляции<br>Закупки к началу: З-4 (стиральная машина), З-5 (сантехника) | К-7: Места стиральной машины в квартире не было. |
| Р-5 | Коробки скрытых дверей, затем штукатурка стен и откосов (стадия 6) | Р-2, Р-3, Р-4 | до начала: электрика и сантехника смонтированы, штробы заделаны; коробки скрытых дверей установлены до штукатурки (поэтому заказ дверей — раньше работы)<br>Закупки к началу: З-1 (двери скрытого монтажа) | К-5: Основа альбома — план заказчика без контрольного обмера: размеры помещений сняты с плана, высота потолка 2700 мм и толщины стен (наружные 250 мм, перегородки 120 мм) приняты — на плане они не указаны. |
| Р-6 | Стяжка пола и тёплый пол (стадия 7) | Р-5 | до начала: штукатурка сделана; трубы под стяжкой приняты; нивелировка плиты выполнена | |
| Р-7 | Гидроизоляция санузлов и тест проливом (стадия 8) | Р-6 | до начала: стяжка набрала прочность и сухая по инструкции гидроизоляции; выводы стоят на проектных отметках | |
| Р-8 | ГКЛ: короба инсталляции и стояков, ниши, потолки (стадия 9) | Р-3, Р-4 | до начала: черновые сети в зоне коробов приняты; закладные под тяжёлое и карнизы стоят; светильники выбраны (вырезы) | |

**Допущения и предложения на листе**

Основа листа: размеры сняты с плана заказчика, контрольный обмер не выполнен (К-5); высота потолка 2700 мм принята: на плане заказчика не указана (К-5); подрайон климата не задан — принят не северный (жилые от 2,5 м) (К-4); толщины стен приняты: наружные 250 мм, перегородки 120 мм — не обмерены (К-5); разрешённая мощность 15 кВт принята по типовой квартире, технических условий нет (К-6).

См. лист открытых вопросов (лист 6, записи К-4–К-6).

| Изм. | Кол.уч | Лист | № док. | Подп. | Дата |
|---|---|---|---|---|---|
| Разраб. | | Кырлан А.С. | | | 04.11.26 |
| Пров. | | | | | |
| ГИП | | | | | |
| | | | | | |
| Н. контр. | | | | | |
| Утв. | | | | | |

**ГД-2026-006-АИ**

Квартира 58 м²

Общая площадь 55,23* м² · * размеры приняты, не замерены (реестр — л. 6, 7, К-5)

Дизайн-проект интерьера

| Стадия | Лист | Листов |
|---|---|---|
| РП | 12 | 87 |

**График закупок и работ. Лист 2 из 3**

М б/м

**Кырлан Александр Сергеевич**

выпуск 04.11.2026 № 3da8f16a26 · стр. 12 из 96

# График закупок и работ. Лист 3 из 3

**ПРЕДВАРИТЕЛЬНО · не для производства работ · открыто пунктов: 10 (реестр — л. 6, 7)**

Что заказывать и когда не раньше чего: относительный порядок без дат; срок поставки — из данных или «не задан» с записью реестра

## Работы: порядок и что не даёт начать (продолжение)

| № | Работа (стадия технологической последовательности) | После | Что должно быть к началу: условия и закупки | Не начинать, пока открыто в реестре |
|---|---|---|---|---|
| Р-9 | Плитка и керамогранит: стены, затем пол; фартук (стадия 10) | Р-6, Р-7, Р-8 | до начала: гидроизоляция принята; плитка выбрана, калибр партии измерен, раскладка пересчитана и подписана<br>Закупки к началу: З-6 (плитка) | |
| Р-10 | Шпаклёвка стен и потолков под окраску (стадия 11) | Р-5, Р-8, Р-9 | до начала: плитка готова (грязные работы закончены); штукатурка и ГКЛ сухие | |
| Р-11 | Окраска стен, потолков, откосов (стадия 13) | Р-10 | до начала: шпаклёвка отшлифована и огрунтована; выкрасы утверждены, колеровка одной партией | |
| Р-12 | Чистовые полы: инженерная доска (стадия 14) | Р-9, Р-11 | до начала: влажность основания в норме, мокрые работы закончены; доска выбрана и привезена<br>Закупки к началу: З-7 (доска и плинтус) | |
| Р-13 | Полотна межкомнатных дверей, плинтусы, пороги (стадия 15) | Р-11, Р-12 | до начала: чистовой пол уложен; полотна скрытых дверей — после чистовой отделки стен | |
| Р-14 | Чистовая электрика и сантехника: механизмы, светильники, смесители, приборы (стадия 16) | Р-11, Р-13 | до начала: отделка готова; механизмы, светильники и приборы выбраны и привезены | |
| Р-15 | Кухня, встроенная и корпусная мебель, бытовая техника (стадия 17) | Р-13, Р-14 | до начала: чистовая сантехника и электрика подведены к местам мебели; замер кухни снят по готовым стенам (после штукатурки или плитки, до чистового пола)<br>Закупки к началу: З-2 (кухонный гарнитур), З-3 (техника кухни), З-8 (мебель по замеру) | К-5: Основа альбома — план заказчика без контрольного обмера: размеры помещений сняты с плана, высота потолка 2700 мм и толщины стен (наружные 250 мм, перегородки 120 мм) приняты — на плане они не указаны. |
| Р-16 | Сдача: осмотр по чек-листу, дефектная ведомость, устранение замечаний (стадия 18) | Р-14, Р-15 | до начала: всё смонтировано; акты скрытых работ подписаны | |

## Примечания

1. Порядок работ — стадии технологической последовательности из 16 позиций, присутствующих в этом проекте (по строкам ведомости объёмов); остальные стадии таблицы knowledge/remont-tehnologiya.md в проекте не встречаются. Длительности работ не печатаются: их нет ни в данных, ни в нормах для этого объекта.
2. Типовые сроки — ориентир практики, не срок поставщика: скрытые двери — короб около 10 дн., полотно под покраску до 3 нед., шпон 4–5 нед., в среднем около 30 дн. (knowledge/workers/foreman.md, п. 2.4 (profil-doors)); кухня и корпусная мебель — 4–8 недель от замера (knowledge/remont-tehnologiya.md, разд. 2; knowledge/workers/foreman.md, п. 2.4). Заказ по ориентиру не назначается: срок получают у поставщика (вопрос реестра), после чего заказ планируют «не позднее чем за срок до начала работы».
3. Условия заказа берутся из реестра открытых вопросов и задания на контрольный обмер: позиция заказывается, когда закрыты замер (графа 1) и решение (графа 2). Закрывать их может только факт или решение автора с подписью; снять строку с листа можно только закрыв запись реестра.
4. Заказ по размеру до контрольного обмера не делают: двери, кухня и встроенная мебель зависят от обмера (К-11, К-13); скрытые двери, кроме того, зависят от решения по нише санузла 2 (проём Д-5 в перегородке П-1).
5. Номера листов — по ведомости рабочих чертежей комплекта (лист «Общие данные»).

**Допущения и предложения на листе**

Основа листа: размеры сняты с плана заказчика, контрольный обмер не выполнен (К-5); высота потолка 2700 мм принята: на плане заказчика не указана (К-5); подрайон климата не задан — принят не северный (жилые от 2,5 м) (К-4); толщины стен приняты: наружные 250 мм, перегородки 120 мм — не обмерены (К-5); разрешённая мощность 15 кВт принята по типовой квартире, технических условий нет (К-6).

См. лист открытых вопросов (лист 6, записи К-4–К-6).

| Изм. | Кол.уч | Лист | № док. | Подп. | Дата |
|---|---|---|---|---|---|
| Разраб. | | Кырлан А.С. | | | 04.11.26 |
| Пров. | | | | | |
| ГИП | | | | | |
| | | | | | |
| Н. контр. | | | | | |
| Утв. | | | | | |

**ГД-2026-006-АИ**

Квартира 58 м²

Общая площадь 55,23* м² · * размеры приняты, не замерены (реестр — л. 6, 7, К-5)

Дизайн-проект интерьера

| Стадия | Лист | Листов |
|---|---|---|
| РП | 13 | 87 |

**График закупок и работ. Лист 3 из 3**

М б/м

**Кырлан Александр Сергеевич**

выпуск 04.11.2026 № 3da8f16a26 · стр. 13 из 96

01

# Архитектурные решения




Кырлан Александр Сергеевич

выпуск 04.11.2026 № 3da8f16a26 · стр. 14 из 96

# Обмерный план

Существующее положение · размеры в мм · отметки от чистого пола

**ПРЕДВАРИТЕЛЬНО · не для производства работ · открыто пунктов: 10 (реестр — л. 6, 7)**

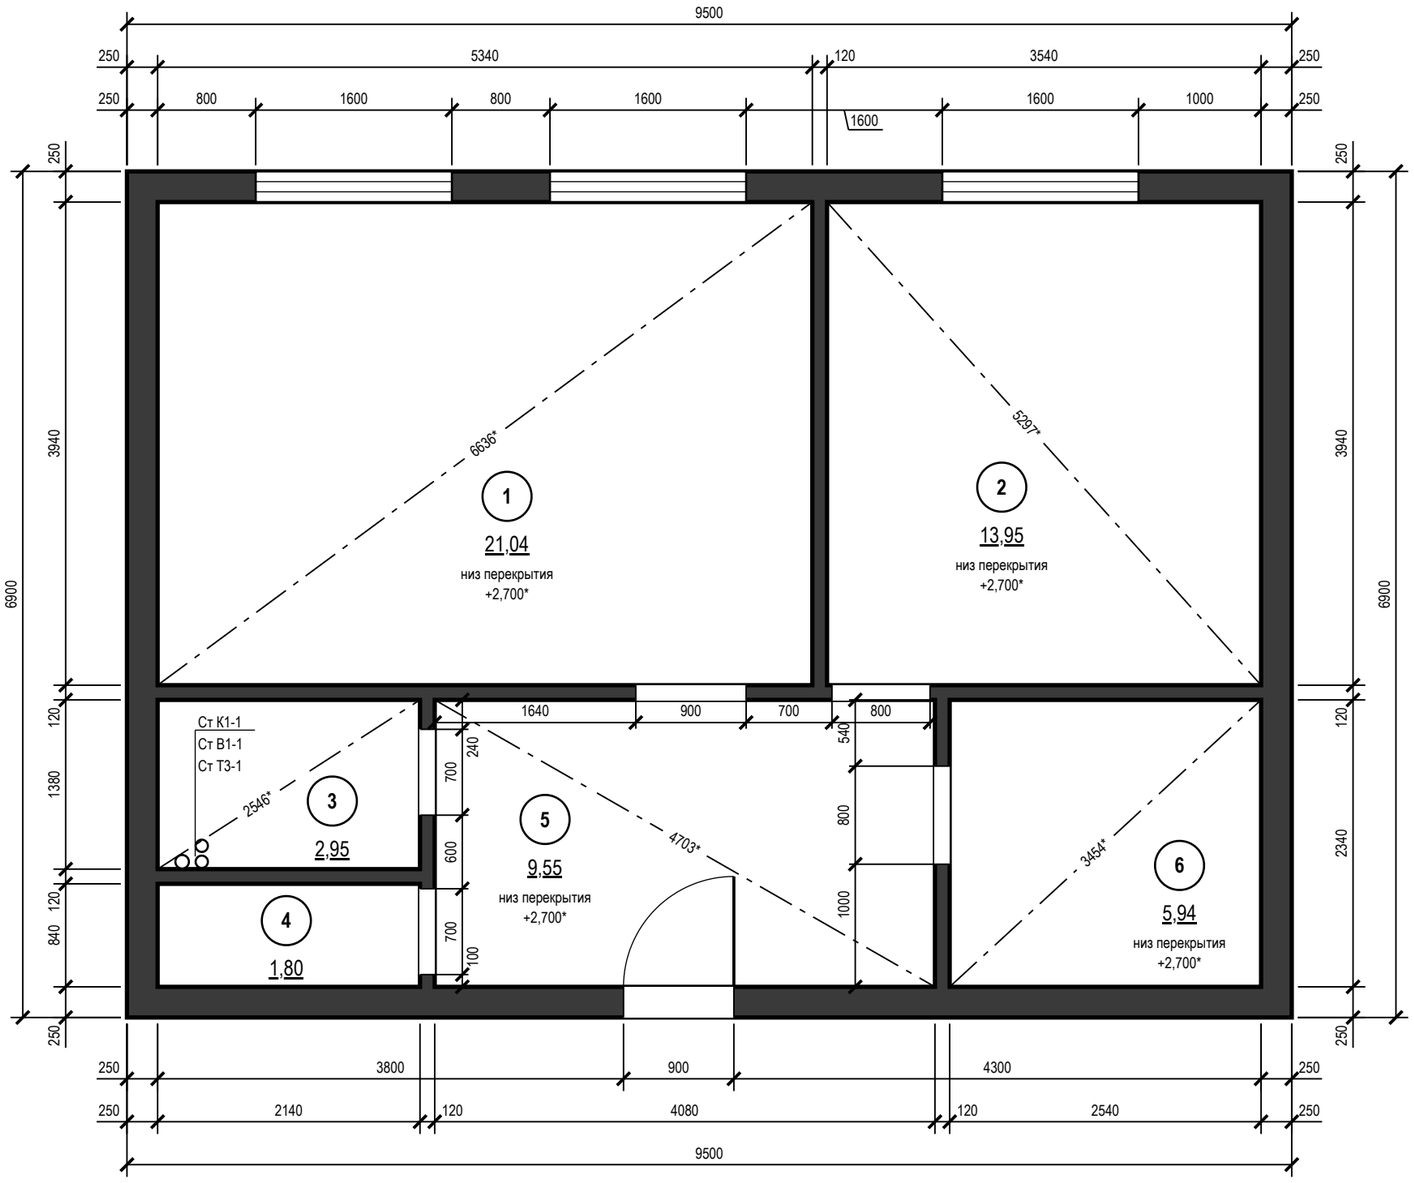


## Экспликация помещений

| № | Наименование | Площадь, м² |
|---|---|---|
| 1 | Кухня-гостиная | 21,04 |
| 2 | Спальня | 13,95 |
| 3 | Ванная | 2,95 |
| 4 | Санузел | 1,80 |
| 5 | Прихожая | 9,55 |
| 6 | Гардеробная | 5,94 |
| | **Итого (общая площадь)** | **55,23** |

## Условные обозначения

- существующие стены (сечение)
- окно (рама, остекление)
- проём существующий, без заполнения (откосы)
- стояк: К1 — канализация, В1 — ХВС, Т3 — ГВС
- диагональ помещения — контроль прямоугольности
- (1) номер помещения, площадь м²

## Примечания

1. Размеры — в мм по чистым поверхностям стен до отделки (по плану заказчика); площади — в м² по тем же размерам. До начала работ выполнить контрольный обмер.
2. За отметку ±0,000 принят чистый пол, не существующий (блок отметок). «Низ перекрытия» у марки помещения — отметка низа перекрытия от ±0,000, как на развёртках и плане потолков (не высота потолка: потолок — по плану потолков); отметка со знаком «*» — принятая, не замер (вопрос К-5).
3. Толщины стен: наружные 250 мм, перегородки 120 мм; отличающиеся толщины и уступы размерами на плане.
4. Несущие стены не определены: до технического заключения все стены считать несущими; проёмы и штробы в них не выполнять.
5. Дверные проёмы показаны без заполнения (двери — лист 16); высота дверных проёмов 2100 мм; низ окон (подоконник) 800 мм от чистого пола, высота окон 1600 мм.
6. Диагонали — контрольные размеры; «*» — расчёт по принятому контуру (К-5), при обмере заменить замеренным; расхождение более 5 мм подписать на плане как перекос.
7. Размеры проверить на месте до начала работ; расхождение контрольных промеров ≤ 2 %.
8. Размеры короче 1 мм на листе цепочкой не показаны (две выносные линии на таком расстоянии сливаются): пом. 5, стена А — 40 мм от проёма до угла.

## Отметки по высоте

| | |
|---|---|
| **±0,000** | чистый пол пом. 1, 2, 5, 6; отсчёт высот |
| **−0,015** | чистый пол пом. 3, 4, ниже на 15 мм |
| **−0,064*** | верх плиты — расчёт, не замер (задание на обмер) |
| **сущ. пол** | снимается до плиты; не замерен (задание на обмер) |

**Допущения и предложения на листе**

Основа листа: размеры сняты с плана заказчика, контрольный обмер не выполнен (К-5); высота потолка 2700 мм принята: на плане заказчика не указана (К-5); подрайон климата не задан — принят не северный (жилые от 2,5 м) (К-4); толщины стен приняты: наружные 250 мм, перегородки 120 мм — не обмерены (К-5); разрешённая мощность 15 кВт принята по типовой квартире, технических условий нет (К-6).

Открытые вопросы и конфликты по листу: К-5.

См. лист открытых вопросов (лист 6, записи К-4–К-6).

1000 мм · печать 1:1

| Изм. | Кол.уч | Лист | № док. | Подп. | Дата |
|---|---|---|---|---|---|
| Разраб. | | Кырлан А.С. | | | 04.11.26 |
| Пров. | | | | | |
| ГИП | | | | | |
| Н. контр. | | | | | |
| Утв. | | | | | |

**ГД-2026-006-АИ**

Квартира 58 м²

Общая площадь 55,23* м² · * размеры приняты, не замерены (реестр — л. 6, 7, К-5)

Дизайн-проект интерьера

| Стадия | Лист | Листов |
|---|---|---|
| РП | 14 | 87 |

**Обмерный план**


М 1:50

**Кырлан Александр Сергеевич**

выпуск 04.11.2026 № 3da8f16a26 · стр. 15 из 96

# План демонтажа и монтажа перегородок


Перепланировка не выполняется · существующие стены сохраняются · размеры в мм

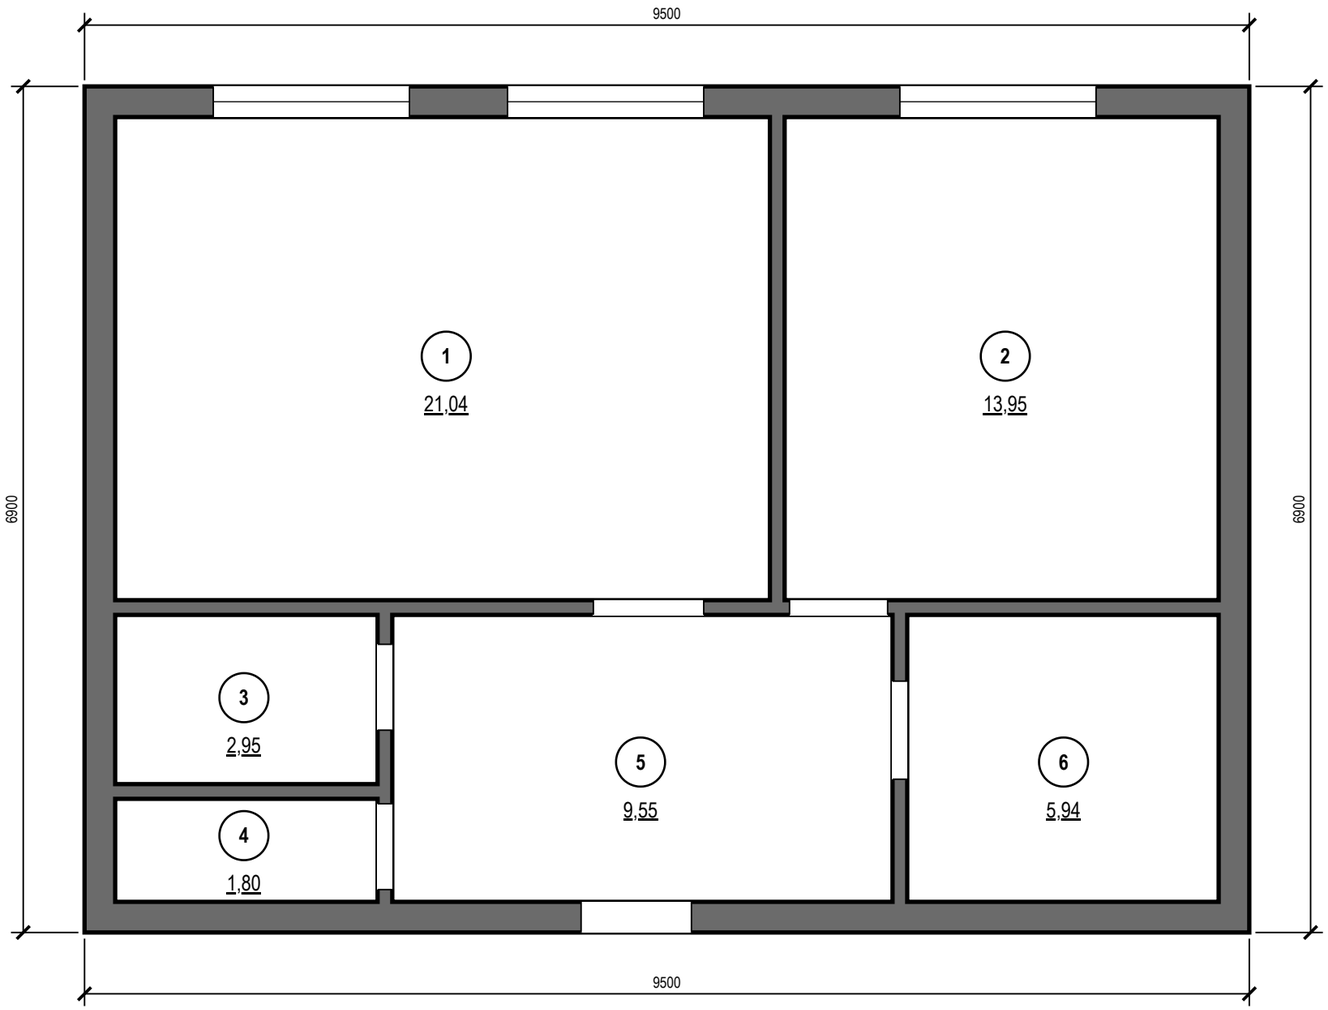


## Условные обозначения

- существующие стены — сохраняются;
- несущие не определены — считать несущими
- демонтируемые конструкции — на плане нет
- возводимые перегородки — на плане нет
- проём существующий, без заполнения (откосы)
- (1) номер помещения, площадь м²

## Отметки по высоте

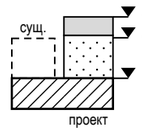


| | |
|---|---|
| **±0,000** | чистый пол пом. 1, 2, 5, 6; отсчёт высот |
| **−0,015** | чистый пол пом. 3, 4, ниже на 15 мм |
| **−0,064*** | верх плиты — расчёт, не замер (задание на обмер) |
| **сущ. пол** | снимается до плиты; не замерен (задание на обмер) |

## Примечания

1. Перепланировка не выполняется: несущие и ненесущие стены, перегородки и плиты перекрытия не демонтируются, новые стены не возводятся; существующие стены и перегородки сохраняются.
2. Дверные блоки — по плану дверей (лист 16); существующие проёмы не расширяются.
3. Демонтаж существующих покрытий пола, стен и потолка, дверных блоков и сантехприборов (если есть) — до основания; объёмы демонтажа — для справки, по факту на объекте.
4. За отметку ±0,000 принят чистый пол, не существующий (блок отметок). Размеры — в мм по чистовой поверхности стен до отделки.
5. Размеры проверить на месте до начала работ: расхождение с обмером — не более 2 % (иначе — к архитектору).
6. Несущие стены не определены: до технического заключения все стены считать несущими — проёмы, ниши и штробы в них не выполнять.

**Допущения и предложения на листе**

Основа листа: размеры сняты с плана заказчика, контрольный обмер не выполнен (К-5); высота потолка 2700 мм принята: на плане заказчика не указана (К-5); подрайон климата не задан — принят не северный (жилые от 2,5 м) (К-4); толщины стен приняты: наружные 250 мм, перегородки 120 мм — не обмерены (К-5); разрешённая мощность 15 кВт принята по типовой квартире, технических условий нет (К-6).

См. лист открытых вопросов (лист 6, записи К-4–К-6).

1000 мм · печать 1:1

| Изм. | Кол.уч | Лист | № док. | Подп. | Дата |
|---|---|---|---|---|---|
| Разраб. | | Кырлан А.С. | | | 04.11.26 |
| Пров. | | | | | |
| ГИП | | | | | |
| Н. контр. | | | | | |
| Утв. | | | | | |

**ГД-2026-006-АИ**

Квартира 58 м²

Общая площадь 55,23* м² · * размеры приняты, не замерены (реестр — л. 6, 7, К-5)

| Дизайн-проект интерьера | Стадия | Лист | Листов |
|---|---|---|---|
| | РП | 15 | 87 |

**План демонтажа и монтажа перегородок**

М 1:50

**Кырлан Александр Сергеевич**

выпуск 04.11.2026 № 3da8f16a26 · стр. 16 из 96

# План дверей и ведомость заполнения проёмов

Проёмы, марки заполнения, привязки · размеры в мм




## Условные обозначения

- стены (подложка обмера)
- дверь распашная, дуга открывания
- дверь скрытого монтажа
- дверь входная (полотно толще)
- оконный блок
- Д — марка типа (Д-N, ОК-N)
- 1 — номер помещения, площадь м²

## Примечания

1. Размеры проёмов и привязки — в миллиметрах от чистых граней стен до отделки; привязка — от угла того помещения, со стороны которого стоит размер. Размер проёма — ширина × высота от чистого пола 0,000. Размеры на плане — проёмов, не полотен: полотно — в ведомости, коробка — по системе. Откос от угла помещения до проёма с коробкой — не менее 50 мм.
2. Марки в кружках — типы заполнения проёмов (ГОСТ 21.501-2018, п. 5.3.2); одна марка — один типоразмер; количество сверено с планом.
3. Открывание: Л — петли слева, П — справа, если смотреть со стороны, куда открывается полотно (на себя).
4. Скрытые двери (Д-2…Д-4): проём замерить в чистоте; блок заказать до штукатурки (≈ 30 дн.), короб ставить до штукатурки; полотно навесить после чистовой отделки, красить в цвет стен. Порядок практика монтажа, изготовитель подтверждает.
5. Д-2…Д-4 — существующие проёмы, до техзаключения не расширять (К-3).
6. Полотно «расч.» — по проёму с запасом по каталогам, заказ — по таблице проёмов модели; Д-2…Д-4: проём 2100, а под полотно 2000 по каталогам нужен 2050–2080, под 2100 — 2150–2180: высоту проёма по модели; Д-1: входной блок по ГОСТ 31173-2016 — задать при выборе блока.
7. Экспликация помещений — лист 14; в марках помещений — номер и площадь, м².
8. Привязка проёма к углу помещения меньше 1 мм на листе, размер на плане не показан: Д-3 — 40 мм; Д-4 — 40 мм.

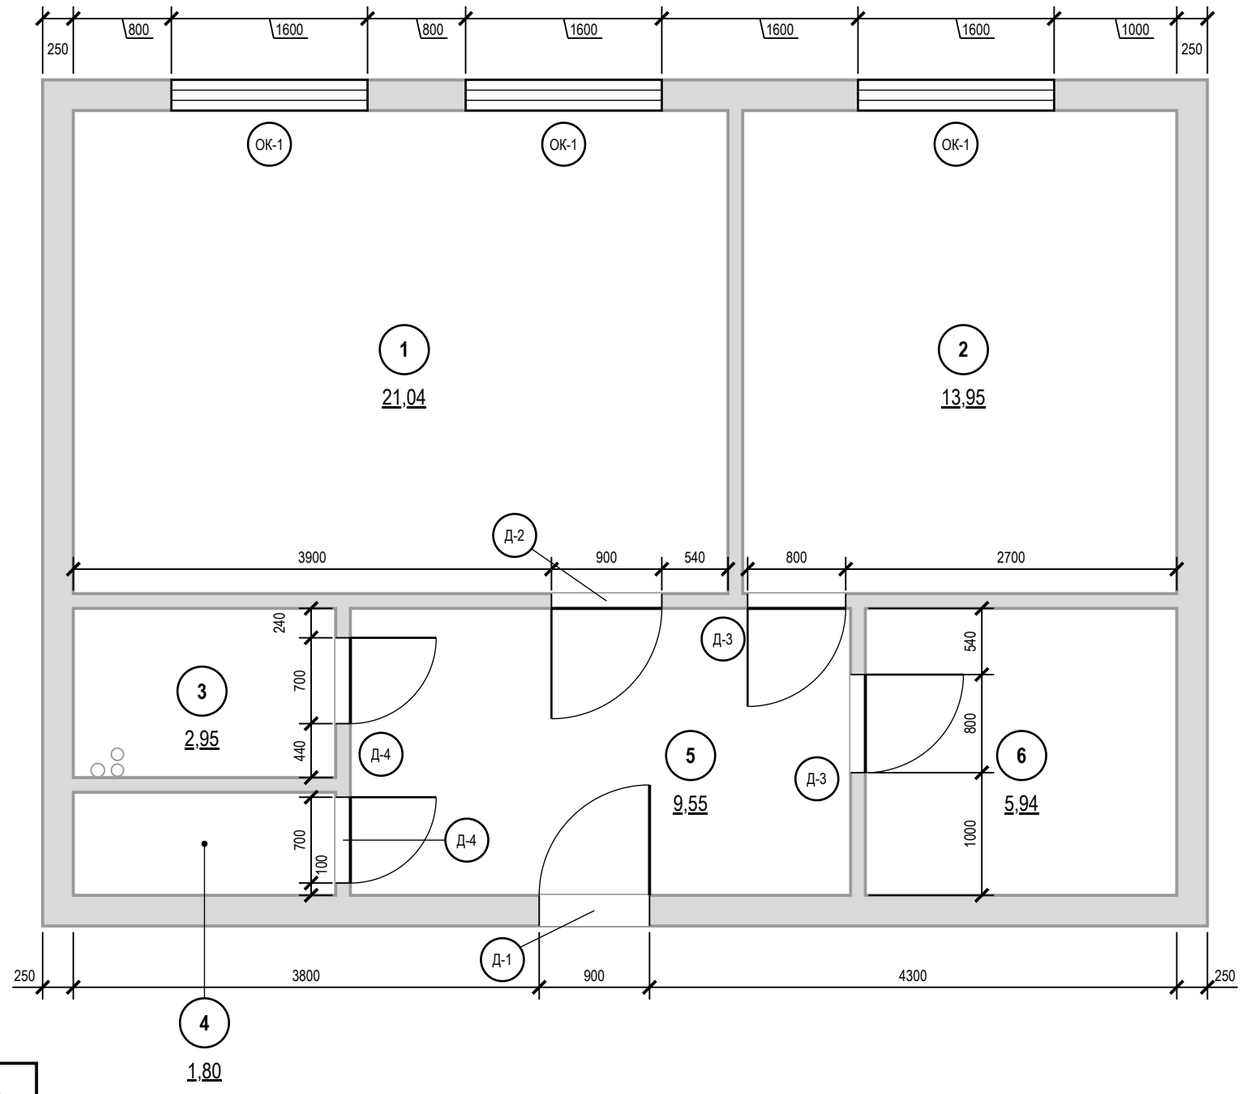


## Ведомость заполнения проёмов

| Марка | Наименование, обозначение | Проём ш×в, мм | Полотно (расч.) | Кол. | Откр. | Отделка полотна | Фурнитура | Прим. |
|---|---|---|---|---|---|---|---|---|
| Д-1 | Блок дверной входной, ГОСТ 31173-2016 | 900×2100 | блок задать | 1 | Л | в комплекте блока | в комплекте блока (замки, глазок) | |
| Д-2 | Дверь скрытого монтажа, Софья (SOFIA) Скрытые двери | 900×2100 | 800×2000 | 1 | Л | S 1502-Y50R — пом. 5, S 1002-Y50R — пом. 1 | скрытые петли 3D, магнитный замок | |
| Д-3 | Дверь скрытого монтажа, Софья (SOFIA) Скрытые двери | 800×2100 | 700×2000 | 2 | Л, П | окраска S 1502-Y50R с двух сторон; V503 пом. 6, S 1502-Y50R пом. 5 | скрытые петли 3D, магнитный замок | |
| Д-4 | Дверь скрытого монтажа, Софья (SOFIA) Скрытые двери | 700×2100 | 600×2000 | 2 | П, П | S 1502-Y50R — пом. 5, в тон облицовки — пом. 3; S 1502-Y50R — пом. 5, в тон облицовки пом. 4 | скрытые петли 3D, магнитный замок, фиксатор WC | порог 15 |
| ОК-1 | Блок оконный, ГОСТ 23166-2021 | 1600×1600 | | 3 | | | | низ 800 |

**Допущения и предложения на листе**

Основа листа: размеры сняты с плана заказчика, контрольный обмер не выполнен (К-5); высота потолка 2700 мм принята: на плане заказчика не указана (К-5); подрайон климата не задан — принят не северный (жилые от 2,5 м) (К-4); толщины стен приняты: наружные 250 мм, перегородки 120 мм — не обмерены (К-5); разрешённая мощность 15 кВт принята по типовой квартире, технических условий нет (К-6).

Открытые вопросы и конфликты по листу: К-3.

См. лист открытых вопросов (лист 6, записи К-3–К-6).

| Изм. | Кол.уч | Лист | № док. | Подп. | Дата |
|---|---|---|---|---|---|
| Разраб. | | Кырлан А.С. | | | 04.11.26 |
| Пров. | | | | | |
| ГИП | | | | | |
| | | | | | |
| Н. контр. | | | | | |
| Утв. | | | | | |

**ГД-2026-006-АИ**

Квартира 58 м²

Общая площадь 55,23* м² · * размеры приняты, не замерены (реестр — л. 6, 7, К-5)

Дизайн-проект интерьера

| Стадия | Лист | Листов |
|---|---|---|
| РП | 16 | 87 |

**План дверей и ведомость заполнения проёмов**

М 1:50

**Кырлан Александр Сергеевич**

1000 мм · печать 1:1

02

# Планировочное решение

Кырлан Александр Сергеевич

выпуск 04.11.2026 № 3da8f16a26 · стр. 18 из 96


# Концепция интерьера

Скандинавский · схема нейтральная · 60/30/10 · материалы, образы и зонирование

## Идея

Стиль — скандинавский: светло, спокойно, уютно (hygge), естественно, функционально, в меру (lagom). Палитра выведена из выкрасов (колерная карта): база — тёплые нейтрали NCS S 1502-Y50R / S 1002-Y50R на стенах, NCS S 0300-N на потолках; второй цвет — Tikkurila V503 (гардеробная); акцент — пыльный синий NCS S 4010-R90B в текстиле по концепции стиля (текстиль в данных ещё не задан). Цветовая схема — нейтральная, пропорция 60/30/10: база на стенах и потолках, вторичный цвет — в текстиле и мягкой мебели, акцент — точечно.

## Мудборд: материалы и фактуры

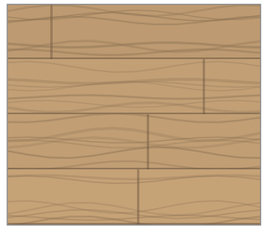

Инженерная доска, дуб натуральный
пол



SG651622R
пол



NCS S 0300-N
потолок, плинтус



NCS S 1502-Y50R
стены



NCS S 1002-Y50R
стены



Winter · Tikkurila V503
стены, потолок, плинтус



610015000370
стены

## Палитра 60/30/10

| | 60 % | | 30 % | 10 % |
|---|---|---|---|---|

60 % база — NCS S 1502-Y50R, LRV 72; NCS S 1002-Y50R, LRV 82; NCS S 0300-N, LRV 92

30 % вторичный — Tikkurila V503 Winter, LRV 86

10 % акцент — NCS S 4010-R90B, LRV 27

## Функциональное зонирование (М 1:100)




- дневная зона: гостиная, кухня, столовая
- мокрая зона: санузлы
- вход и коммуникации
- (1) номер помещения (лист 18)
- ночная зона: спальни
- хранение: гардеробная, кладовая
- функциональная зона в помещении

## Образы помещений

**1. Кухня-гостиная** — 21,04 м²

стены NCS S 1002-Y50R
пол — доска, дуб натуральный
свет 3000 K

**2. Спальня** — 13,95 м²

стены NCS S 1502-Y50R
пол — доска, дуб натуральный
свет 2700 K

**5. Прихожая** — 9,55 м²

стены NCS S 1502-Y50R
пол — SG651622R
свет 3000 K

**6. Гардеробная** — 5,94 м²

стены Tikkurila V503
пол — доска, дуб натуральный
свет 3000 K

**3. Ванная** — 2,95 м²

стены Italon 610015000370
пол — SG651622R
свет 3000 K

**4. Санузел** — 1,80 м²

стены Italon 610015000370
пол — SG651622R
свет 3000 K

## Материалы и отделка

**Инженерная доска, дуб натуральный**
масло, 1-полосная, 14/4 мм
пол — пом. 1, 2, 6

**SG651622R**
пол — пом. 3, 4, 5

**610015000370**
стены — пом. 3, 4

**NCS S 1002-Y50R, LRV 82**
стены — пом. 1

**NCS S 0300-N, LRV 92**
глубокоматовая
потолок, плинтус — пом. 1, 2, 3, 4, 5

**NCS S 1502-Y50R, LRV 72**
глубокоматовая
стены — пом. 2, 5

**Tikkurila V503 Winter, LRV 86**
Tikkurila Harmony, матовая
стены, потолок, плинтус — пом. 6

## Чего избегаем

1) Холодный белый + серый ламинат + серый диван без дерева
2) Принты олени/Hygge, надписи, лишние подушки
3) Глянцевый лак на дереве, венге, под орех
4) Одна люстра на комнату, свет 4000–6500 K, споты сеткой
5) Тяжёлые шторы с ламбрекенами, лепнина, многоуровневые потолки
6) Три разных светлых дуба в одном помещении

**Допущения и предложения на листе**

Основа листа: размеры сняты с плана заказчика, контрольный обмер не выполнен (К-5); высота потолка 2700 мм принята: на плане заказчика не указана (К-5); подрайон климата не задан — принят не северный (жилые от 2,5 м) (К-4); толщины стен приняты: наружные 250 мм, перегородки 120 мм — не обмерены (К-5); разрешённая мощность 15 кВт принята по типовой квартире, технических условий нет (К-6).
См. лист открытых вопросов (лист 6, записи К-4–К-6).

## Примечания

1. Коды цвета — по веерам производителей (колерная карта, лист 49); перед закупкой краски — выкрас на стене объекта под дневным светом и лампами проекта.
2. Материалы — по ведомости отделки (лист 48); мебель, текстиль и декор — по спецификации (лист 19). Образцы доски, керамогранита и тканей утвердить до заказа.
3. Фактуры на листе условные, цвет передан по HEX-значениям производителей: при печати возможны отклонения, решение — только по физическому образцу.

| Изм. | Кол.уч | Лист | № док. | Подп. | Дата |
|---|---|---|---|---|---|
| Разраб. | | Кырлан А.С. | | | 04.11.26 |
| Пров. | | | | | |
| ГИП | | | | | |
| Н. контр. | | | | | |
| Утв. | | | | | |

**ГД-2026-006-АИ**

Квартира 58 м²

Общая площадь 55,23* м² · * размеры приняты, не замерены (реестр — л. 6, 7, К-5)

Дизайн-проект интерьера

| Стадия | Лист | Листов |
|---|---|---|
| РП | 17 | 87 |

**Концепция интерьера**

М б/м


**Кырлан Александр Сергеевич**

выпуск 04.11.2026 № 3da8f16a26 · стр. 19 из 96

# План расстановки мебели

Мебель и оборудование · размеры в мм от чистовых стен · марки — по ведомости



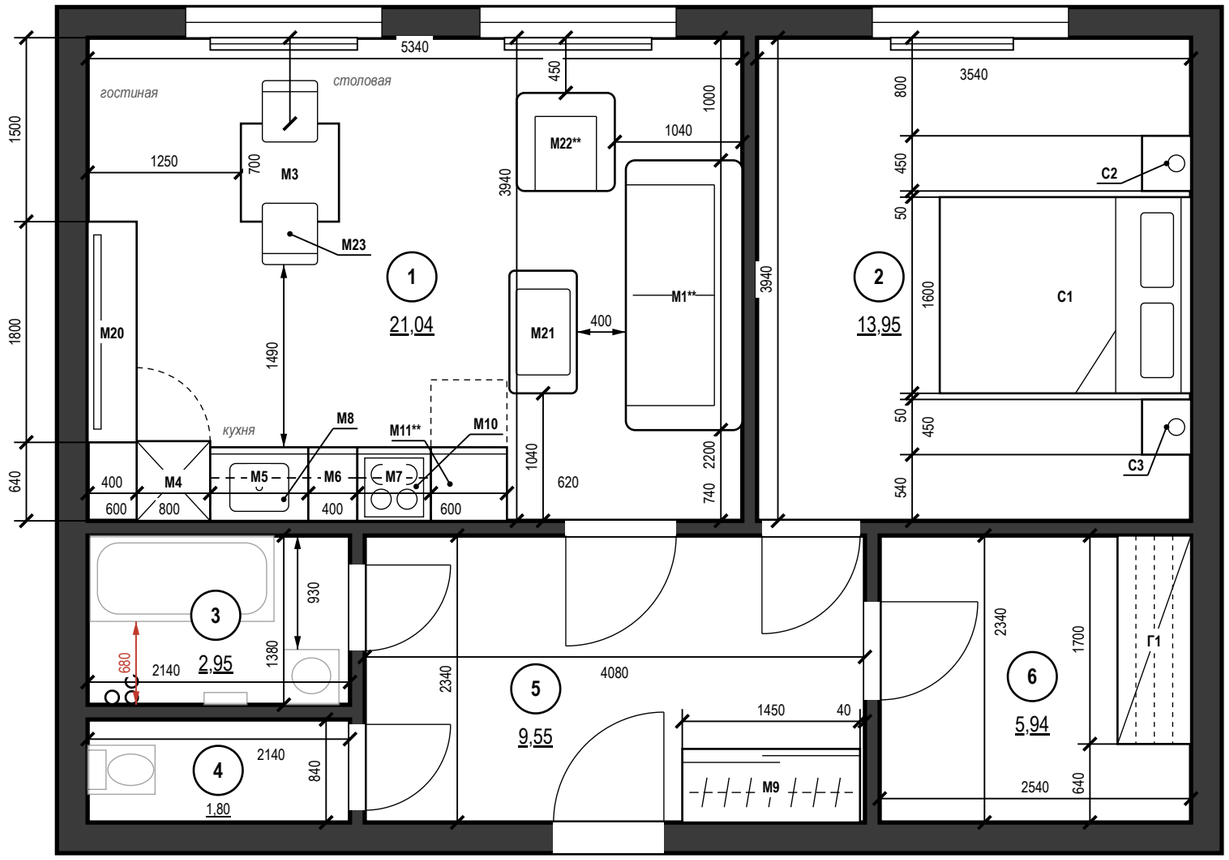


**Экспликация помещений**

лист 14 · на плане — номера в марках

## Ведомость мебели и оборудования

| Марка | Наименование | Ш×Г×В, мм | Пом. | Кол. |
|---|---|---|---|---|
| M4 | Пенал кухонный | 600×650×2100 | 1 | 1 |
| M5 | Модуль нижний | 800×600×900 | 1 | 1 |
| M6 | Модуль нижний | 400×600×900 | 1 | 1 |
| M7 | Модуль нижний | 600×600×900 | 1 | 1 |
| M11** | Ниша под стиральную машину | 620×600×900 | 1 | 1 |
| M8 | Модуль навесной | 1200×350×720 | 1 | 1 |
| M10 | Навесной модуль над варочной | 600×350×620 | 1 | 1 |
| M1** | Диван | 2200×950×850 | 1 | 1 |
| M3 | Стол обеденный | 800×800×750 | 1 | 1 |
| M20 | ТВ-тумба подвесная с экраном | 1800×400×450 | 1 | 1 |
| M21 | Стол журнальный | 550×1000×400 | 1 | 1 |
| M22** | Кресло | 800×800×800 | 1 | 1 |
| C1 | Кровать двуспальная | 1600×2050×450 | 2 | 1 |
| C2 | Тумба прикроватная | 450×400×500 | 2 | 1 |
| C3 | Тумба прикроватная | 450×400×500 | 2 | 1 |
| M9 | Шкаф-купе | 1450×600×2450 | 5 | 1 |
| Г1 | Система хранения | 1700×600×2400 | 6 | 1 |
| M23 | Стул обеденный к столу M3 | 450×500×820 | 1 | 2 |

Ш — вдоль стены (изголовья), Г — от стены (длина кровати)

Материалы, модели, допуск замены — лист 19

## Условные обозначения

- мебель и оборудование — габарит в масштабе
- навесные шкафы (низ выше 0,9 м) — невидимый контур
- зона открывания дверец шкафов и техники
- **К1** — марка предмета по ведомости мебели
- привязка от чистовой стены, мм
- ширина прохода, зазор, мм
- проход меньше нормы — расстановку изменить
- сантехприборы — подложка (лист ВК)
- радиатор отопления (лист ОВ)
- существующие стены (сечение)
- стояк: К1 — канализация, В1 — ХВС, Т3 — ГВС
- (1) — номер помещения, площадь м²
- *зона* — функциональная зона помещения

## Примечания

1. Размеры — в мм от чистовых поверхностей стен, размеры помещений — в свету, привязки — от стен, углов помещения и соседних предметов, проходы и зазоры — стрелками; розетки и выводы под мебель — лист 20, выключатели — лист 22, сантехприборы — лист 29.
2. Общие указания к расстановке (чистовой слой, контрольный обмер, зазоры встроенной мебели, замена покупной) — примечания к спецификации, лист 19.
3. Стулья обеденной группы (M23 — 2 шт.) показаны в рабочем положении, задвинутыми под столешницу на 150 мм.

**Допущения и предложения на листе**

Основа листа: размеры сняты с плана заказчика, контрольный обмер не выполнен (К-5); высота потолка 2700 мм принята: на плане заказчика не указана (К-5); подрайон климата не задан — принят не северный (жилые от 2,5 м) (К-4); толщины стен приняты: наружные 250 мм, перегородки 120 мм — не обмерены (К-5); разрешённая мощность 15 кВт принята по типовой квартире, технических условий нет (К-6).

Знак «**» — предложение проектировщика, заказчиком не утверждено (согласовать с заказчиком): ИЗ-2: M1 — Было offset 1300…3500: торец дивана в 500 мм от стены В, правые 350 мм проёма Д-2 (3900…4800) упирались в диван; M22 — Было x 4250 — место занял диван M1 (x 4450…5400 от y 1000); К-7: M11 — место стиральной машины: вместо модуля с ящиками 400 справа от варочной; ряд до 3420, журнальный стол M21 (с x 3440) не мешает загрузке.

Открытые вопросы и конфликты по листу: К-2, К-7.

Изменения по листу без подписи: ИЗ-2.

См. лист открытых вопросов (лист 6, записи К-2, К-4–К-7; лист 7, запись ИЗ-2).

1000 мм · печать 1:1

| Изм. | Кол.уч | Лист | № док. | Подп. | Дата |
|---|---|---|---|---|---|
| Разраб. | | Кырлан А.С. | | | 04.11.26 |
| Пров. | | | | | |
| ГИП | | | | | |
| | | | | | |
| Н. контр. | | | | | |
| Утв. | | | | | |

**ГД-2026-006-АИ**

Квартира 58 м²

Общая площадь 55,23* м² · * размеры приняты, не замерены (реестр — л. 6, 7, К-5)

Дизайн-проект интерьера

| Стадия | Лист | Листов |
|---|---|---|
| РП | 18 | 87 |

**План расстановки мебели**

М 1:50

**Кырлан Александр Сергеевич**

выпуск 04.11.2026 № 3da8f16a26 · стр. 20 из 96

# Спецификация мебели и оборудования

**ПРЕДВАРИТЕЛЬНО · не для производства работ · открыто пунктов: 10 (реестр — л. 6, 7)**

Форма 1 ГОСТ 21.110-2013 · позиции мебели — по плану расстановки

| Поз. | Наименование и техническая характеристика | Тип, марка, обозначение документа, опросного листа | Код продукции | Поставщик | Ед. измерения | Кол. | Масса 1 ед., кг | Примечание |
|---|---|---|---|---|---|---|---|---|
| | **Мебель встроенная и корпусная (изготовление по чертежам мебельщика)** | | | | | | | |
| М4 | Пенал кухонный, холодильник; корпус ЛДСП 16 мм; фасады — без фасада (прибор отдельностоящий); Ш×Г×В 600×650×2100 мм | | | изготовление на заказ | шт. | 1 | | пом. 1 |
| М5 | Модуль нижний, мойка; корпус ЛДСП 16 мм; фасады — МДФ эмаль 18 мм; Ш×Г×В 800×600×900 мм | | | изготовление на заказ | шт. | 1 | | пом. 1 |
| М6 | Модуль нижний; корпус ЛДСП 16 мм; фасады — МДФ эмаль 18 мм; Ш×Г×В 400×600×900 мм | | | изготовление на заказ | шт. | 1 | | пом. 1 |
| М7 | Модуль нижний, варочная; корпус ЛДСП 16 мм; фасады — МДФ эмаль 18 мм; Ш×Г×В 600×600×900 мм | | | изготовление на заказ | шт. | 1 | | пом. 1 |
| М8 | Модуль навесной; корпус ЛДСП 16 мм; фасады — МДФ эмаль 18 мм; Ш×Г×В 1200×350×720 мм | | | изготовление на заказ | шт. | 1 | | пом. 1 |
| М10 | Навесной модуль над варочной, вытяжка встраивается в дно; корпус ЛДСП 16 мм; фасады — МДФ эмаль 18 мм; Ш×Г×В 600×350×620 мм | | | изготовление на заказ | шт. | 1 | | пом. 1 |
| М11** | Модуль под встраиваемую ПММ 60; без корпуса (ниша между соседними модулями); фасад на дверь машины — МДФ эмаль 18 мм; цоколь; Ш×Г×В 620×600×900 мм | | | изготовление на заказ | шт. | 1 | | пом. 1 |
| М9 | Шкаф-купе; корпус ЛДСП 16 мм; фасады — ЛДСП 10 мм в алюминиевом профиле; Ш×Г×В 1450×600×2450 мм | | | изготовление на заказ | шт. | 1 | | пом. 5 |
| Г1 | Система хранения: штанги, полки, ящики; каркас и полки — ЛДСП 16 мм, декор «дуб натуральный»; без фасадов; Ш×Г×В 1700×600×2400 мм | | | изготовление на заказ | шт. | 1 | | пом. 6; крепление к стене |
| | **Мебель покупная** | | | | | | | |
| М1** | Диван; обивка — ткань, цвет Tikkurila V503; Ш×Г×В 2200×950×850 мм | | | аналог по характеристикам | шт. | 1 | | пом. 1; замена ≤ габарита |
| М3 | Стол обеденный; шпон, дуб натуральный, матовое масло; Ш×Г×В 800×800×750 мм | | | аналог по характеристикам | шт. | 1 | | пом. 1; замена ≤ габарита |
| М20 | ТВ-тумба подвесная с экраном; шпон, дуб натуральный, матовое масло; Ш×Г×В 1800×400×450 мм | | | аналог по характеристикам | шт. | 1 | | пом. 1; замена ≤ габарита |
| М21 | Стол журнальный; шпон, дуб натуральный, матовое масло; Ш×Г×В 550×1000×400 мм | | | аналог по характеристикам | шт. | 1 | | пом. 1; замена ≤ габарита |
| М22** | Кресло; обивка — ткань, цвет Tikkurila V503; Ш×Г×В 800×800×800 мм | | | аналог по характеристикам | шт. | 1 | | пом. 1; замена ≤ габарита |
| М23 | Стул обеденный к столу М3; обивка — ткань, цвет Tikkurila V503; каркас — дуб натуральный; Ш×Г×В 450×500×820 мм | | | аналог по характеристикам | шт. | 2 | | пом. 1; замена ≤ габарита |
| С1 | Кровать двуспальная; мягкое изголовье, обивка — ткань, цвет Tikkurila V503; Ш×Г×В 1600×2050×450 мм | | | аналог по характеристикам | шт. | 1 | | пом. 2; замена ≤ габарита |
| С2, С3 | Тумба прикроватная; шпон, дуб натуральный, матовое масло; Ш×Г×В 450×400×500 мм | | | аналог по характеристикам | шт. | 2 | | пом. 2; замена ≤ габарита |
| | **Техника встраиваемая и бытовая (покупные изделия), светильники под розетки** | | | | | | | |
| | Холодильник, в модуле М4 | аналог по характеристикам: отдельностоящий, габарит — по проёму | | по выбору заказчика до изготовления мебели | шт. | 1 | | пом. 1; по схеме изготовителя |
| | Варочная панель встраиваемая, индукционная, в модуле М7 | аналог по характеристикам: индукционная 60 см, вырез 560 × 490 мм по шаблону модели | | по выбору заказчика до изготовления мебели | шт. | 1 | | пом. 1; по схеме изготовителя |
| | Стиральная машина, в модуле М11** | аналог по характеристикам: тип загрузки — по листу ВК, по листу ВК | | по выбору заказчика до изготовления мебели | шт. | 1 | | пом. 1; по схеме изготовителя |
| | Вытяжка встраиваемая, в модуле М10 | аналог по характеристикам: производительность — по расчёту ОВ, шум ≤ 55 дБ(А) | | по выбору заказчика до изготовления мебели | шт. | 1 | | пом. 1; по схеме изготовителя |
| | Торшер, у поз. М3; абажур — ткань или опаловое стекло; лампа 3000 К | | | аналог по характеристикам | шт. | 1 | | пом. 1; розетка — по плану розеток (ЭОМ) |

## Примечания

1. Позиции мебели совпадают с марками на плане расстановки (лист 18); размеры Ш×Г×В — Ш вдоль стены, Г от стены.
2. Размеры и привязки плана расстановки — в мм от чистовых поверхностей стен: слой штукатурки 20 мм по блоку и 5 мм шпаклёвки по ГКЛ учтён; привязки — от стен и углов помещения, а не от другой мебели.
3. План расстановки не является документацией для изготовления мебели. Встроенная и корпусная мебель изготавливается по чертежам мебельщика после контрольного обмера (после штукатурки); «стена в стену» — с зазором 10 мм с каждой стороны или с компенсаторами; графы «Тип, марка» и «Код продукции» для неё не заполняются (ГОСТ 21.110-2013).
4. Покупные изделия — аналог по характеристикам: заменять только на изделия не больше указанного габарита и того же материала и цвета.
5. Материал и цвет, не указанные в данных изделия, приняты по концепции (лист 17): тон дерева — по полу, обивка — по вторичному цвету палитры; образцы согласовать до заказа.
6. Масса 1 ед. для изделий до 25 кг не указывается. Техника — по монтажным схемам изготовителя; выводы — по листам ЭОМ и ВК.

**Допущения и предложения на листе**

Основа листа: размеры сняты с плана заказчика, контрольный обмер не выполнен (К-5); высота потолка 2700 мм принята: на плане заказчика не указана (К-5); подрайон климата не задан — принят не северный (жилые от 2,5 м) (К-4); толщины стен приняты: наружные 250 мм, перегородки 120 мм — не обмерены (К-5); разрешённая мощность 15 кВт принята по типовой квартире, технических условий нет (К-6).

Знак «**» — предложение проектировщика, заказчиком не утверждено (согласовать с заказчиком): ИЗ-2: М1 — Было offset 1300…3500: торец дивана в 500 мм от стены В, правые 350 мм проёма Д-2 (3900…4800) упирались в диван; М22 — Было х 4250 — место занял диван М1 (х 4450…5400 от у 1000); К-7: М11 — место стиральной машины: вместо модуля с ящиками 400 справа от варочной; ряд до 3420, журнальный стол М21 (с х 3440) не мешает загрузке.

Изменения по листу без подписи: ИЗ-2.

См. лист открытых вопросов (лист 6, записи К-4–К-7; лист 7, запись ИЗ-2).

| Изм. | Кол.уч | Лист | № док. | Подп. | Дата |
|---|---|---|---|---|---|
| Разраб. | | Кырлан А.С. | | | 04.11.26 |
| Пров. | | | | | |
| ГИП | | | | | |
| Н. контр. | | | | | |
| Утв. | | | | | |

**ГД-2026-006-АИ**

Квартира 58 м²

Общая площадь 55,23* м² · * размеры приняты, не замерены (реестр — л. 6, 7, К-5)

Дизайн-проект интерьера

| Стадия | Лист | Листов |
|---|---|---|
| РП | 19 | 87 |

**Спецификация мебели и оборудования**

М б/м

**Кырлан Александр Сергеевич**

выпуск 04.11.2026 № 3da8f16a26 · стр. 21 из 96

03

# Электрооборудование


Кырлан Александр Сергеевич

выпуск 04.11.2026 № 3da8f16a26 · стр. 22 из 96

# План розеток и электровыводов

Розетки, выводы кабеля, щит · размеры в мм · высоты от чистого пола

**ПРЕДВАРИТЕЛЬНО · не для производства работ · открыто пунктов: 10 (реестр — л. 6, 7)**

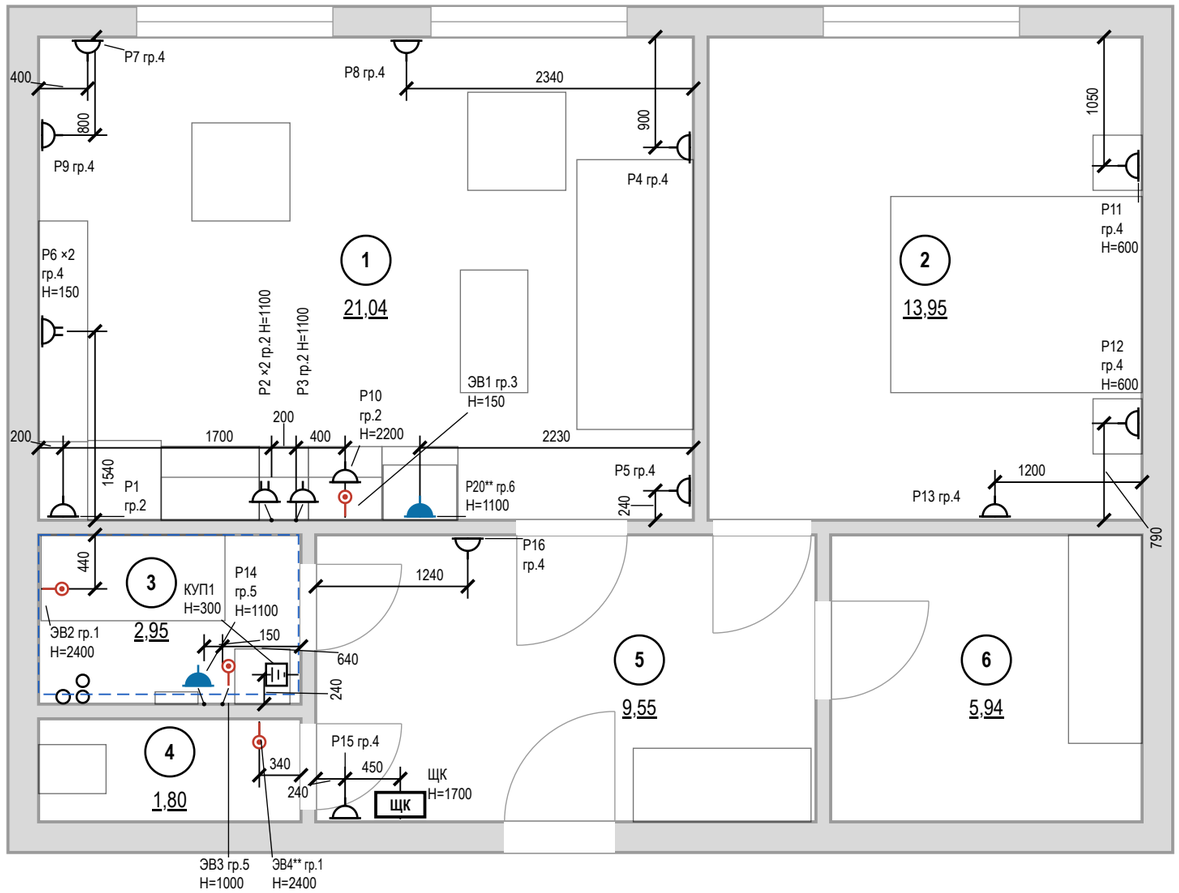


## Условные обозначения

| Знак | Тип изделия | Н, мм | Кол., шт |
|---|---|---|---|
| | Розетка с заземлением | 300 | 9 |
| | То же | у знака | 4 |
| | Блок розеток с заземлением, рамка 2 поста | у знака | 2 |
| | Розетка с заземлением IP44 | 1100 | 2 |
| | Вывод кабеля к прибору | у знака | 4 |
| | КУП (уравнивание потенциалов) | 300 | 1 |
| ЩК | Щит квартирный | 1700 | 1 |

розетка с заземляющим контактом; у знака — марка, ×N — постов в рамке, гр. — группа щита, Н — высота оси, мм

знак разведён для читаемости: точка на стене — у выноски, привязка — до неё

граница зоны 2 ванной (600 мм от ванны/поддона)

мебель и сантехприборы — подложка

стояк: К1 — канализация, В1 — ХВС, Т3 — ГВС

1 — номер помещения, площадь м²

**Итого розеток (механизмов) — 19 шт; рамок — 17 шт: на 1 пост — 15, на 2 поста — 2.**

**Допущения и предложения на листе**

Основа листа: размеры сняты с плана заказчика, контрольный обмер не выполнен (К-5); высота потолка 2700 мм принята: на плане заказчика не указана (К-5); подрайон климата не задан — принят не северный (жилые от 2,5 м) (К-4); толщины стен приняты: наружные 250 мм, перегородки 120 мм — не обмерены (К-5); разрешённая мощность 15 кВт принята по типовой квартире, технических условий нет (К-6).

Знак «**» — предложение проектировщика, заказчиком не утверждено (согласовать с заказчиком): ЭВ4 — вывод к бытовому вентилятору, таймер выбега; К-7: Р20 — питание стиральной машины П6 — отдельная группа 6 (УЗО 30 мА); над столешницей в габарите машины, не за корпусом.

Изменения по листу без подписи: ИЗ-1.

См. лист открытых вопросов (лист 6, записи К-4–К-7; лист 7, запись ИЗ-1).

## Примечания

1. За отметку 0,000 принят уровень чистого пола. Высоты Н — от чистого пола до оси изделия; привязки — от чистовой грани стены до оси механизма (у рамки на несколько постов — до оси рамки).
2. Розетки без отметки Н у знака — на высоте 300 мм от чистого пола до оси механизма; выводы кабеля — по паспорту прибора.
3. Розетки в санузле — только вне зон 0–2 (ПУЭ 7.1.48, ГОСТ Р 50571.7.701-2024), IP44, через УЗО 30 мА.
4. Розеточные и мокрые линии — через УЗО или дифавтомат с током утечки не более 30 мА (ПУЭ 7.1.79); в санузле выполнить ДСУП (ПУЭ 7.1.87–7.1.88).
5. Кабель — медный, исполнение нг(А)-LS (ГОСТ 31565-2012); скрытая прокладка только горизонтально и вертикально, фактические трассы зафиксировать исполнительной схемой до закрытия отделкой.
6. Расчёт нагрузок, токов КЗ, селективности и сечений — по проекту ЭОМ организации с допуском СРО; лист задаёт состав, расположение и группы.
7. Выводы кухонной техники — после утверждения проекта кухни (ориентировочно); привязки выводов даны от осей модулей гарнитура и пересматриваются вместе с проектом кухни.
8. Ведомости электроточек, изделий, светильников и расшифровка клавиш — лист 23.

1000 мм · печать 1:1

| Изм. | Кол.уч | Лист | № док. | Подп. | Дата |
|---|---|---|---|---|---|
| Разраб. | | Кырлан А.С. | | | 04.11.26 |
| Пров. | | | | | |
| ГИП | | | | | |
| | | | | | |
| Н. контр. | | | | | |
| Утв. | | | | | |

**ГД-2026-006-АИ**

Квартира 58 м²

Общая площадь 55,23* м² · * размеры приняты, не замерены (реестр — л. 6, 7, К-5)

Дизайн-проект интерьера

| Стадия | Лист | Листов |
|---|---|---|
| РП | 20 | 87 |

**План розеток и электровыводов**

М 1:50


**Кырлан Александр Сергеевич**

выпуск 04.11.2026 № 3da8f16a26 · стр. 23 из 96

# План освещения

Светильники, группы включения, извещатели · размеры в мм

**ПРЕДВАРИТЕЛЬНО · не для производства работ · открыто пунктов: 10 (реестр — л. 6, 7)**

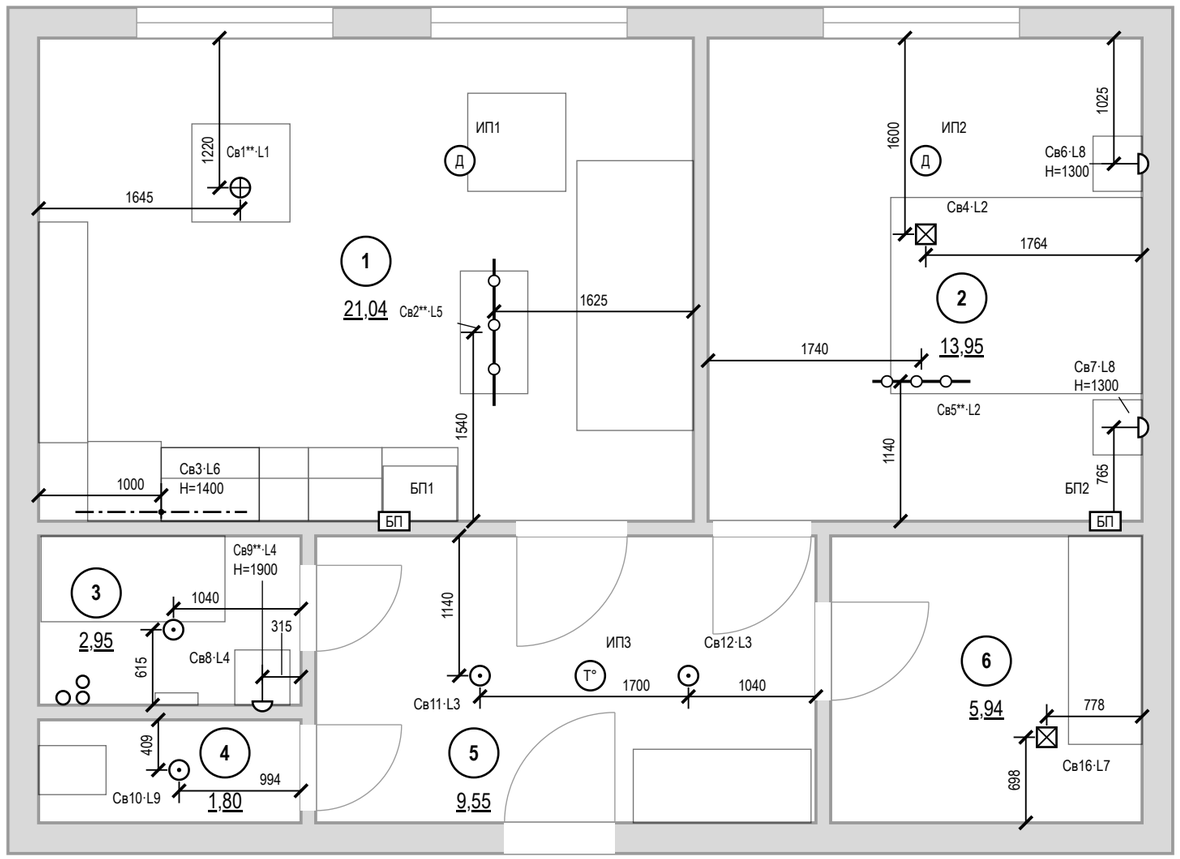


## Условные обозначения

- светильник встраиваемый точечный
- светильник потолочный накладной
- светильник подвесной
- светильник настенный (бра), H — высота оси
- линейный светильник настенный (подсветка столешницы), точка — вывод питания
- трековая система
- Св1·L1 — марка светильника (как в ведомости и на развёртках) · группа включения L (лист 22)
- Д — извещатель пожарный дымовой автономный
- Т° — извещатель пожарный тепловой
- БП — блок питания LED, с доступом (люк от 100×100 мм)
- мебель и сантехприборы — подложка
- стояк: К1 — канализация, В1 — ХВС, Т3 — ГВС
- 1 — номер помещения, площадь м²

**Допущения и предложения на листе**

Основа листа: размеры сняты с плана заказчика, контрольный обмер не выполнен (К-5); высота потолка 2700 мм принята: на плане заказчика не указана (К-5); подрайон климата не задан — принят не северный (жилые от 2,5 м) (К-4); толщины стен приняты: наружные 250 мм, перегородки 120 мм — не обмерены (К-5); разрешённая мощность 15 кВт принята по типовой квартире, технических условий нет (К-6).

Знак «**» — предложение проектировщика, заказчиком не утверждено (согласовать с заказчиком): Св2 — общий свет зоны гостиной над журнальным столом М21 (трек шёл вдоль края стола М3 по проходу); трековая система 4 × 950 лм: поток принят до нормы освещённости, модель и паспорт не выбраны; Св5 — трековая система 2 × 900 лм: светильник добавлен проектировщиком, поток принят до нормы освещённости, модель и паспорт не выбраны; Св1 — подвес висел над проходом без заданной высоты, а стол — без света над ним: подвес по оси стола М3; Св9 — свет у зеркала — над зеркалом у умывальника по его оси (свет на лицо, а не над сантехникой).

Изменения по листу без подписи: ИЗ-1.

См. лист открытых вопросов (лист 6, записи К-4–К-6; лист 7, запись ИЗ-1).

## Примечания

1. За отметку 0,000 принят уровень чистого пола. Высоты H — от чистого пола до оси изделия; привязки — от чистовой грани стены до оси механизма (у рамки на несколько постов — до оси рамки).
2. Высота установки, не указанная на плане: светильники — на потолке; настенные — по отметке H у знака. Привязки — до оси светильника от чистовой грани стены, по рядам.
3. Во влажных помещениях — светильники не ниже IP44; в зонах 0–2 ванной — по ГОСТ Р 50571.7.701-2024 (зона 1 — IPX5).
4. Розеточные и мокрые линии — через УЗО или дифавтомат с током утечки не более 30 мА (ПУЭ 7.1.79); в санузле выполнить ДСУП (ПУЭ 7.1.87–7.1.88).
5. Кабель — медный, исполнение нг(A)-LS (ГОСТ 31565-2012); скрытая прокладка только горизонтально и вертикально, фактические трассы зафиксировать исполнительной схемой до закрытия отделкой.
6. Расчёт нагрузок, токов КЗ, селективности и сечений — по проекту ЭОМ организации с допуском СРО; лист задаёт состав, расположение и группы.
7. Ведомость светильников (тип, количество, мощность, поток, Тц, Ra) — лист 39.
8. Оценка освещённости (по норме СанПиН 1.2.3685-21, табл. 5.52, на полу; не светотехнический расчёт, декоративная подсветка в оценку не входит) — лист 23.


1000 мм · печать 1:1

| | | | | | | | |
|---|---|---|---|---|---|---|---|
| | | | | | | **ГД-2026-006-АИ** | |
| | | | | | | Квартира 58 м² | |
| | | | | | | Общая площадь 55,23* м² · * размеры приняты, не замерены (реестр — л. 6, 7, К-5) | |
| Изм. | Кол.уч | Лист | № док. | Подп. | Дата | Дизайн-проект интерьера | Стадия: РП; Лист: 21; Листов: 87 |
| Разраб. | | Кырлан А.С. | | | 04.11.26 | | |
| Пров. | | | | | | | |
| ГИП | | | | | | | |
| | | | | | | **План освещения** | **Кырлан Александр Сергеевич** |
| Н. контр. | | | | | | М 1:50 | |
| Утв. | | | | | | | |

# План выключателей и схема включения

Выключатели S, группы включения L, линии связи · размеры в мм

**ПРЕДВАРИТЕЛЬНО · не для производства работ · открыто пунктов: 10 (реестр — л. 6, 7)**

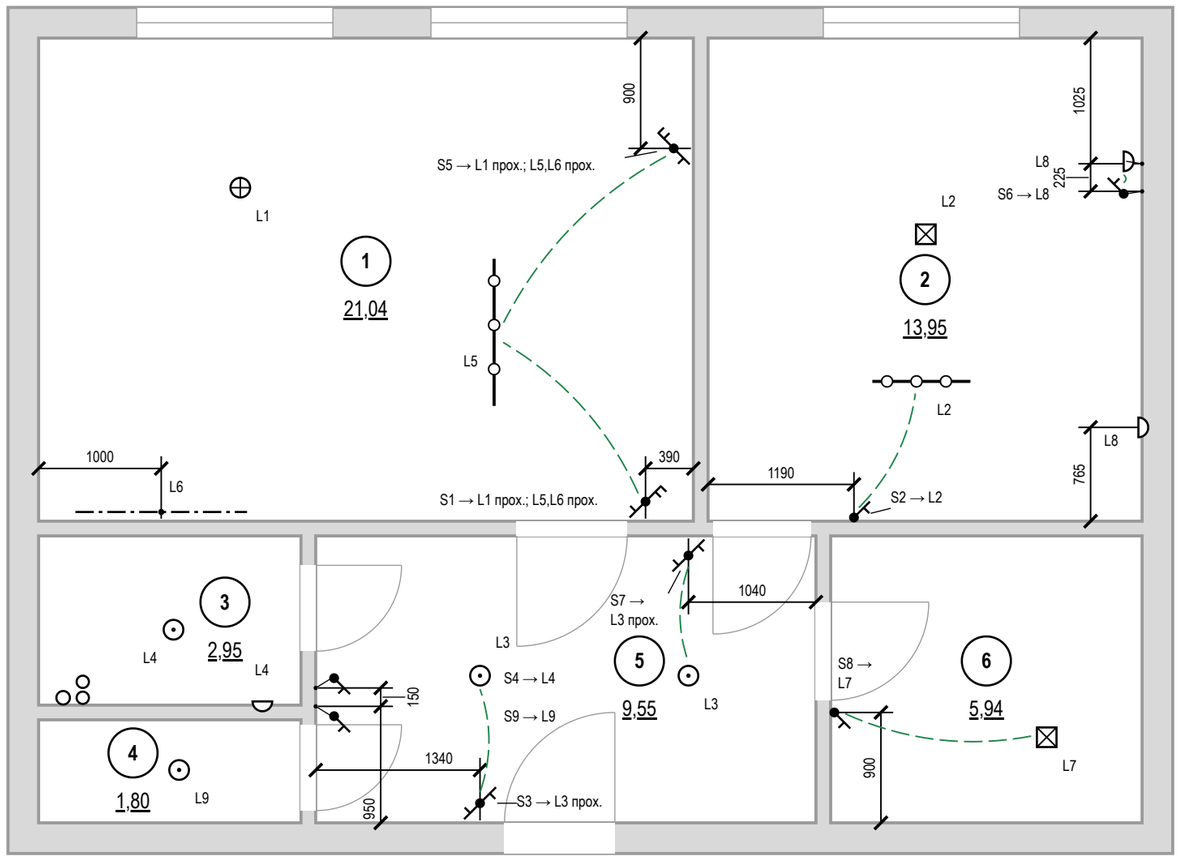


**Допущения и предложения на листе**

Основа листа: размеры сняты с плана заказчика, контрольный обмер не выполнен (К-5); высота потолка 2700 мм принята: на плане заказчика не указана (К-5); подрайон климата не задан — принят не северный (жилые от 2,5 м) (К-4); толщины стен приняты: наружные 250 мм, перегородки 120 мм — не обмерены (К-5); разрешённая мощность 15 кВт принята по типовой квартире, технических условий нет (К-6).

Изменения по листу без подписи: ИЗ-1.

См. лист открытых вопросов (лист 6, записи К-4–К-6; лист 7, запись ИЗ-1).

## Условные обозначения

- выключатель одноклавишный
- выключатель с проходной или перекрёстной клавишей (обратный флажок); тип клавиши — в подписи
- S1 → — марка → группы по клавишам (через «;»): прох. — проходной, перекр. — перекрёстный, дим. — светорегулятор; Н — высота
- связь: выключатель → ближайший светильник группы в том же помещении (не трасса кабеля); полный состав группы — по номеру L
- светильник встраиваемый точечный
- светильник потолочный накладной
- светильник подвесной
- светильник настенный (бра), Н — высота оси
- линейный светильник настенный (подсветка столешницы), точка — вывод питания
- трековая система
- L1 — группа включения у светильника
- стояк: К1 — канализация, В1 — ХВС, Т3 — ГВС
- 1 — номер помещения, площадь м²

## Примечания

1. За отметку 0,000 принят уровень чистого пола. Высоты Н — от чистого пола до оси изделия; привязки — от чистовой грани стены до оси механизма (у рамки на несколько постов — до оси рамки).
2. Высота установки, не указанная на плане: выключатели — 900 мм от чистого пола (у кровати и другие — Н у марки), со стороны дверной ручки (ПУЭ 7.1.51).
3. Какой выключатель какие светильники включает — по номеру группы L: у выключателя (S1 → L1; L2 — клавиши по порядку) и у каждого светильника. Пунктир подсказка к ближайшему светильнику группы в том же помещении (не дальше 3 м), это не трасса кабеля; выключатель за стеной (у двери санузла) и далёкая группа — только номер группы.
4. Группы из нескольких мест (L1 — S1, S5; L5 — S1, S5; L6 — S1, S5; L3 — S3, S7): на крайних местах — проходные клавиши, на промежуточных — перекрёстные; механизмы — в ведомости изделий.
5. Вентиляторы санузлов (выводы ЭВ на плане розеток) включаются вместе с основным светом помещения, отключаются с задержкой — таймер выбега в вентиляторе.
6. Розеточные и мокрые линии — через УЗО или дифавтомат с током утечки не более 30 мА (ПУЭ 7.1.79); в санузле выполнить ДСУП (ПУЭ 7.1.87–7.1.88).
7. Кабель — медный, исполнение нг(А)-LS (ГОСТ 31565-2012); скрытая прокладка только горизонтально и вертикально, фактические трассы зафиксировать исполнительной схемой до закрытия отделкой.
8. Расчёт нагрузок, токов КЗ, селективности и сечений — по проекту ЭОМ организации с допуском СРО; лист задаёт состав, расположение и группы.
9. Расшифровка клавиш и ведомость изделий — лист 23.

1000 мм · печать 1:1

| | | | | | | | |
|---|---|---|---|---|---|---|---|
| | | | | | | **ГД-2026-006-АИ** | |
| | | | | | | Квартира 58 м² | |
| | | | | | | Общая площадь 55,23* м² · * размеры приняты, не замерены (реестр — л. 6, 7, К-5) | |
| Изм. | Кол.уч | Лист | № док. | Подп. | Дата | Дизайн-проект интерьера | Стадия: РП; Лист: 22; Листов: 87 |
| Разраб. | | Кырлан А.С. | | | 04.11.26 | | |
| Пров. | | | | | | | |
| ГИП | | | | | | | |
| Н. контр. | | | | | | **План выключателей и схема включения** М 1:50 | **Кырлан Александр Сергеевич** |
| Утв. | | | | | | | |

выпуск 04.11.2026 № 3da8f16a26 · стр. 25 из 96

# Ведомость электроточек и изделий

Электроточки, изделия, светильники, освещённость, клавиши выключателей · б/м

## Ведомость электроточек

| Марка | Пом. | Назначение | Н, мм | Гр. |
|---|---|---|---|---|
| Р1 | 1 | холодильник | 300 | 2 |
| Р2 | 1 | рабочая зона | 1100 | 2 |
| Р3 | 1 | рабочая зона | 1100 | 2 |
| Р4 | 1 | у дивана | 300 | 4 |
| Р5 | 1 | у дивана | 300 | 4 |
| Р6 | 1 | ТВ, приставка (за тумбой М20) | 150 | 4 |
| Р7 | 1 | торшер | 300 | 4 |
| Р8 | 1 | зона отдыха | 300 | 4 |
| Р9 | 1 | обеденная зона | 300 | 4 |
| Р10 | 1 | вытяжка (встроена в дно М10) | 2200 | 2 |
| Р20** | 1 | стиральная машина, IP44 | 1100 | 6 |
| ЭВ1 | 1 | варочная панель | 150 | 3 |
| Р11 | 2 | розетка общего назначения | 600 | 4 |
| Р12 | 2 | розетка общего назначения | 600 | 4 |
| Р13 | 2 | комод, зарядка | 300 | 4 |
| КУП1 | 3 | КУП | 300 | |
| Р14 | 3 | фен, IP44 | 1100 | 5 |
| ЭВ2 | 3 | вентилятор ВР2 (клавиша L4, таймер выбега) | 2400 | 1 |
| ЭВ3 | 3 | полотенцесушитель, IP44 | 1000 | 5 |
| ЭВ4** | 4 | вентилятор ВР3 (таймер выбега) | 2400 | 1 |
| Р15 | 5 | питание ЩС** (роутер, ИБП) | 300 | 4 |
| Р16 | 5 | уборка | 300 | 4 |
| ЩК | 5 | щит квартирный | 1700 | |

## Ведомость изделий

| Наименование | Марки | Ед. | Кол. |
|---|---|---|---|
| Розетка с з/к и защитными шторками, 16 А | по ведомости точек | шт | 17 |
| Розетка IP44 с крышкой, 16 А | Р14, Р20** | шт | 2 |
| Выключатель 1-клав. | S2, S4, S6, S8, S9 | шт | 5 |
| Выключатель 1-клав. проходной | S3, S7 | шт | 2 |
| Выключатель 2-клав. проходной | S1, S5 | шт | 2 |
| Рамка 1-постовая | в т. ч. 9 под выключ. | шт | 24 |
| Рамка 2-постовая | | шт | 2 |
| Коробка установочная (подрозетник) Ø68 | розетки, выключатели | шт | 28 |
| Вывод кабеля под прибор (клеммник) | ЭВ1–ЭВ3 | шт | 3 |
| Вывод кабеля к вентилятору вытяжки | ЭВ4** | шт | 1 |
| Коробка уравнивания потенциалов КУП | КУП1 | шт | 1 |
| Блок питания LED 24 В, 100 Вт | БП1 | шт | 1 |
| Блок питания LED 24 В, 60 Вт | БП2 | шт | 1 |
| Извещатель дымовой автономный | ИП1, ИП2 | шт | 2 |
| Извещатель тепловой | ИП3 | шт | 1 |
| Щит квартирный (состав — лист щита) | ЩК | шт | 1 |
| Розетка компьютерная RJ45, кат. 6, с рамкой и подрозетником | LAN1, LAN2 | шт | 2 |
| Розетка телевизионная (коаксиальная) с рамкой и подрозетником | ТВ1 | шт | 1 |
| Трубка или монитор домофона (поставка домофонной организации) | ДФ1 | шт | 1 |
| Щит слаботочный ЩС**: корпус, DIN-рейка, розетки 220 В | ЩС** | шт | 1 |
| Патч-панель, портов не менее 2 | | шт | 1 |
| Коммутатор, портов не менее 2, из них PoE 0 | | шт | 1 |
| Кабель домофона — тип по системе поставщика (по лучам от ЩС**, запас 10 %) | | м | 3,4 |
| Кабель коаксиальный RG-6 (75 Ом) к розеткам ТВ (по лучам от ЩС**, запас 10 %) | | м | 16,3 |
| Кабель U/UTP кат. 5e (LAN, Wi-Fi и камеры по PoE) (по лучам от ЩС**, запас 10 %) | | м | 30,1 |

## Ведомость светильников

| Поз. | Марки | Тип | Кол. | Р, Вт | Ф, лм | IP | Тц/Ra |
|---|---|---|---|---|---|---|---|
| 1 | Св1** | подвесной | 1 | 40 | 3600 | | 3000/90 |
| 2 | Св2** | трековая система | 4 | 12 | 950 | | 3000/90 |
| 3 | Св3 | линейный светильник, Н=1400 | 1 | 14 | 1080 | | 3000/90 |
| 4 | Св4 | потолочный накладной | 1 | 36 | 3200 | | 2700/90 |
| 5 | Св5** | трековая система | 2 | 12 | 900 | | 2700/90 |
| 6 | Св6, Св7 | настенный (бра), Н=1300 | 2 | 4 | 250 | | 2700/90 |
| 7 | Св8 | встраиваемый точечный | 1 | 9 | 700 | 44 | 3000/90 |
| 8 | Св9** | настенный (бра), Н=1900 | 1 | 6 | 400 | 44 | 3000/90 |
| 9 | Св10 | встраиваемый точечный | 1 | 6 | 500 | 44 | 3000/90 |
| 10 | Св11, Св12 | встраиваемый точечный | 2 | 9 | 800 | | 3000/90 |
| 11 | Св16 | потолочный накладной | 1 | 10 | 900 | | 3000/90 |

## Освещённость (оценка)

| Пом. | S, м² | Ен, лк | Ф треб., лм | Ф по пр., лм |
|---|---|---|---|---|
| 1 | 21 | 150 | 8890 | 7400 |
| 2 | 13,9 | 150 | 5890 | 5000 |
| 3 | 3 | 50 | 420 | 700 |
| 4 | 1,8 | 50 | 250 | 500 |
| 5 | 9,6 | 50 | 1350 | 1600 |
| 6 | 5,9 | 75 | 1250 | 900 |

## Расшифровка клавиш

| Марка | Пом. | Н, мм | Клав. | Механизм | Группа: светильники |
|---|---|---|---|---|---|
| S1 | 1 | 900 | 1 | проходной | L1: Св1** |
| | | | 2 | проходной | L5: Св2**; L6: Св3 |
| S2 | 2 | 900 | 1 | обычный | L2: Св4, Св5** |
| S3 | 5 | 900 | 1 | проходной | L3: Св11, Св12 |
| S4 | 5 | 900 | 1 | обычный | L4: Св8, Св9** |
| S5 | 1 | 900 | 1 | проходной | L1: Св1** |
| | | | 2 | проходной | L5: Св2**; L6: Св3 |
| S6 | 2 | 900 | 1 | обычный | L8: Св6, Св7 |

## Расшифровка клавиш (продолжение)

| Марка | Пом. | Н, мм | Клав. | Механизм | Группа: светильники |
|---|---|---|---|---|---|
| S7 | 5 | 900 | 1 | проходной | L3: Св11, Св12 |
| S8 | 6 | 900 | 1 | обычный | L7: Св16 |
| S9 | 5 | 900 | 1 | обычный | L9: Св10 + ЭВ4** (вентилятор) |

Допущения и предложения на листе. Основа листа: размеры сняты с плана заказчика, контрольный обмер не выполнен (К-5); высота потолка 2700 мм принята: на плане заказчика не указана (К-5); подрайон климата не задан — принят не северный (жилые от 2,5 м) (К-4); толщины стен приняты: наружные 250 мм, перегородки 120 мм — не обмерены (К-5); разрешённая мощность 15 кВт принята по типовой квартире, технических условий нет (К-6). Знак «**» — предложение проектировщика, заказчиком не утверждено (согласовать с заказчиком): Св2 — общий свет зоны гостиной над журнальным столом М21 (трек шёл вдоль края стола М3 по проходу); трековая система 4 × 950 лм: поток принят до нормы освещённости, модель и паспорт не выбраны; Св5 — трековая система 2 × 900 лм: светильник добавлен проектировщиком, поток принят до нормы освещённости, модель и паспорт не выбраны; Св1 — подвес висел над проходом без заданной высоты, а стол — без света над ним: подвес по оси стола М3; Св9 — свет у зеркала — над зеркалом у умывальника по его оси (свет на лицо, а не над сантехникой); ЩС — щит слаботочный: место и состав; ЭВ4 — вывод к бытовому вентилятору, таймер выбега; К-7: Р20 — питание стиральной машины П6 — отдельная группа 6 (УЗО 30 мА); над столешницей в габарите машины, не за корпусом. См. лист открытых вопросов (лист 6, записи К-4–К-7).

## Примечания

1. Ведомости сведены с планов розеток, освещения и выключателей; марки, группы и высоты — те же, что у знаков на планах.
2. Механизмы, рамки и светорегуляторы — одной серии; число постов и клавиш сверено с выбранной серией. Перекрёстная клавиша — отдельный механизм серии.
3. Освещённость (оценка) — по норме СанПиН 1.2.3685-21 (табл. 5.52, на полу), не светотехнический расчёт; декоративная подсветка в оценку не входит.
4. За отметку 0,000 принят уровень чистого пола. Высоты Н — от чистого пола до оси изделия; привязки — от чистовой грани стены до оси механизма (у рамки на несколько постов — до оси рамки).
5. Розеточные и мокрые линии — через УЗО или дифавтомат с током утечки не более 30 мА (ПУЭ 7.1.79); в санузле выполнить ДСУП (ПУЭ 7.1.87–7.1.88).
6. Кабель — медный, исполнение нг(A)-LS (ГОСТ 31565-2012); скрытая прокладка только горизонтально и вертикально, фактические трассы зафиксировать исполнительной схемой до закрытия отделкой.
7. Расчёт нагрузок, токов КЗ, селективности и сечений — по проекту ЭОМ организации с допуском СРО; лист задаёт состав, расположение и группы.

| Изм. | Кол.уч | Лист | № док. | Подп. | Дата |
|---|---|---|---|---|---|
| Разраб. | | Кырлан А.С. | | | 04.11.26 |
| Пров. | | | | | |
| ГИП | | | | | |
| | | | | | |
| Н. контр. | | | | | |
| Утв. | | | | | |

**ГД-2026-006-АИ**

Квартира 58 м²

Общая площадь 55,23* м² · * размеры приняты, не замерены (реестр — л. 6, 7, К-5)

Дизайн-проект интерьера

| Стадия | Лист | Листов |
|---|---|---|
| РП | 23 | 87 |


**Ведомость электроточек и изделий**

М б/м

**Кырлан Александр Сергеевич**

# Однолинейная схема щита

Щит квартирный ЩК · без масштаба

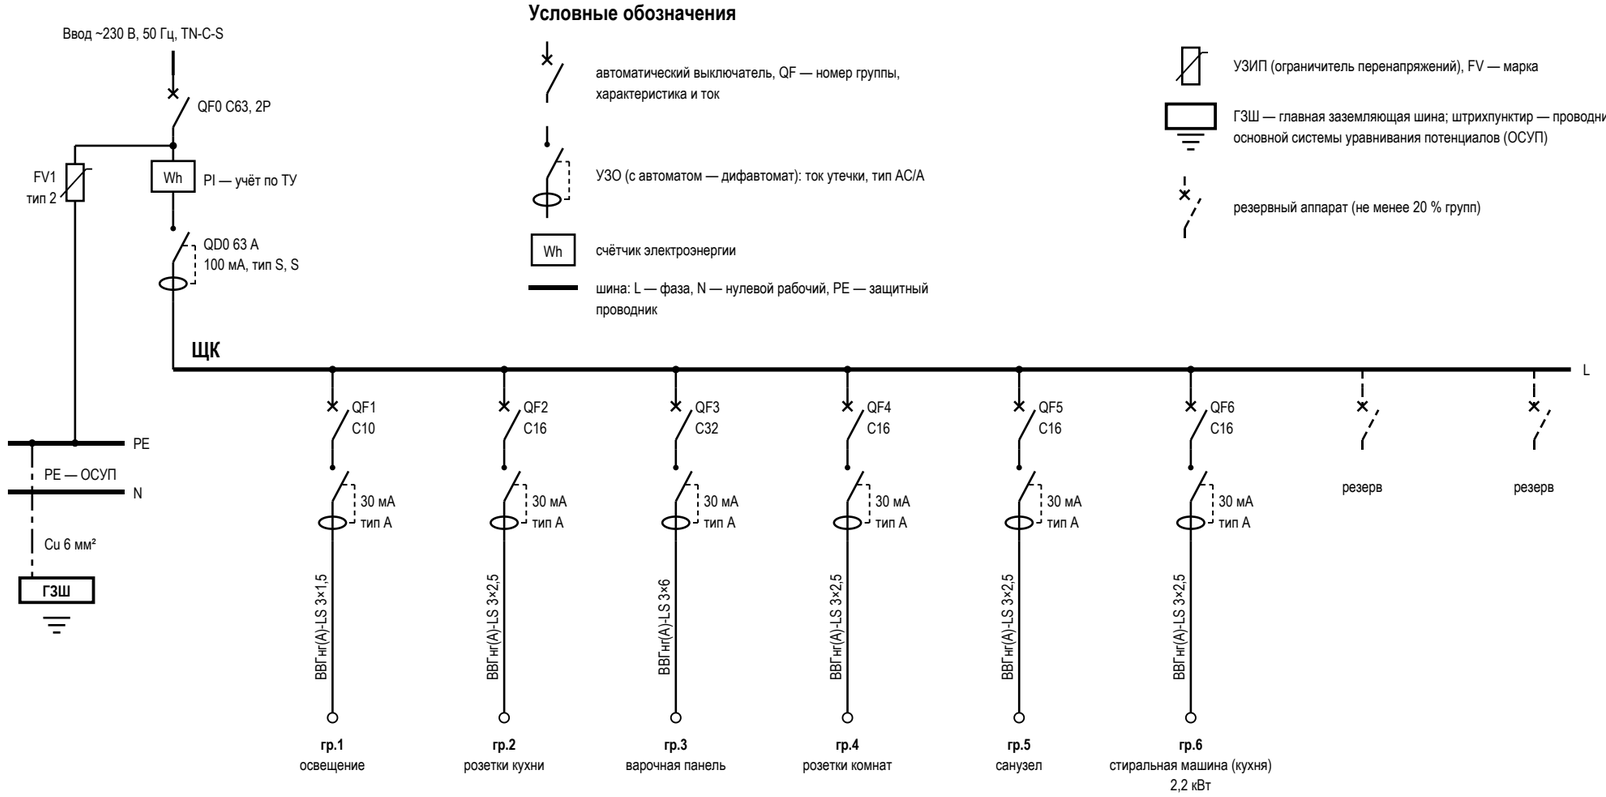


### Условные обозначения

- автоматический выключатель, QF — номер группы, характеристика и ток
- УЗО (с автоматом — дифавтомат): ток утечки, тип AC/A
- Wh — счётчик электроэнергии
- шина: L — фаза, N — нулевой рабочий, PE — защитный проводник
- УЗИП (ограничитель перенапряжений), FV — марка
- ГЗШ — главная заземляющая шина; штрихпунктир — проводник основной системы уравнивания потенциалов (ОСУП)
- резервный аппарат (не менее 20 % групп)

### Данные щитка

| Показатель | Значение |
|---|---|
| Номер щитка | ЩК |
| Тип | ЩРВ-П-24, IP41 |
| Уст. мощность, кВт | |
| Разреш. мощность, кВт | 15 |
| Расчётная, кВт | 9,8 |
| Автоматы 1п: занят. / рез. | 6 / 2 |
| Модулей: всего / занято | 24 / 19 |
| Ток на вводе, А | 63 |
| Вводной аппарат | QF0 C63, 2P |
| УЗИП | FV1, тип 2, ЩК, после счётчика |
| ГЗШ, проводник ОСУП | Cu 6 мм² |

### Таблица групп щита ЩК и кабельный журнал

| № | Назначение | Помещения | Автомат | УЗО / дифавтомат | Кабель | Длина, м | Р, кВт | Точек |
|---|---|---|---|---|---|---|---|---|
| 1 | освещение | 1, 2, 3, 4, 5, 6 | C10 | 30 мА, тип A | ВВГнг(A)-LS 3×1,5 | 105,4 | | 25 |
| 2 | розетки кухни | 1 | C16 | 30 мА, тип A | ВВГнг(A)-LS 3×2,5 | 20,8 | | 4 |
| 3 | варочная панель | 1 | C32 | 30 мА, тип A | ВВГнг(A)-LS 3×6 | 10,7 | | 1 |
| 4 | розетки комнат | 1, 2, 5 | C16 | 30 мА, тип A | ВВГнг(A)-LS 3×2,5 | 48,1 | | 11 |
| 5 | санузел | 3 | C16 | 30 мА, тип A | ВВГнг(A)-LS 3×2,5 | 12 | | 2 |
| 6 | стиральная машина (кухня) | 1 | C16 | 30 мА, тип A | ВВГнг(A)-LS 3×2,5 | 11 | 2,2 | 1 |
| | Итого по сечениям ВВГнг(A)-LS, м: 3×1,5 — 105,4; 3×2,5 — 91,9; 3×6 — 10,7 | | | | | 208 | | |

### Примечания

1. Схема однолинейная: одна линия — фаза, N и PE группы; аппараты — в отключённом положении (ГОСТ 2.702, ГОСТ 2.755). Номера групп — как у точек на планах (гр.). За отметку 0,000 принят уровень чистого пола; высота щита — по плану розеток.
2. Розеточные и мокрые линии — через УЗО или дифавтомат с током утечки не более 30 мА (ПУЭ 7.1.79); в санузле выполнить ДСУП (ПУЭ 7.1.87–7.1.88).
3. УЗО тип A — для линий с электроникой, стиральной и посудомоечной машиной, LED-драйверами; тип AC — только для чисто активной нагрузки.
4. Кабель — медный, исполнение нг(A)-LS (ГОСТ 31565-2012); скрытая прокладка только горизонтально и вертикально, фактические трассы зафиксировать исполнительной схемой до закрытия отделкой.
5. Номинал автомата — не выше допустимого тока кабеля: 1,5 мм² — до 10 А, 2,5 мм² — до 16 А. Резерв щита — не менее 20 % модулей.
6. Расчёт нагрузок, токов КЗ, селективности и сечений — по проекту ЭОМ организации с допуском СРО; лист задаёт состав, расположение и группы.
7. УЗИП FV1 — после вводного автомата, проводник к шине PE — кратчайший, без петель. Шина PE щита соединяется с ГЗШ проводником ОСУП; к ГЗШ присоединяются трубы водопровода и отопления на вводе в квартиру (ПУЭ 7.1.87). Шины N и PE — раздельные, после разделения PEN не объединяются.
8. До подключения нагрузки — приёмо-сдаточные испытания с протоколом: сопротивление изоляции линий не менее 0,5 МОм, срабатывание УЗО по току и времени, непрерывность защитных проводников PE (ПУЭ, гл. 1.8).

**Допущения и предложения на листе**

Основа листа: размеры сняты с плана заказчика, контрольный обмер не выполнен (К-5); высота потолка 2700 мм принята: на плане заказчика не указана (К-5); подрайон климата не задан — принят не северный (жилые от 2,5 м) (К-4); толщины стен приняты: наружные 250 мм, перегородки 120 мм — не обмерены (К-5); разрешённая мощность 15 кВт принята по типовой квартире, технических условий нет (К-6).

Открытые вопросы и конфликты по листу: К-6, К-7.

См. лист открытых вопросов (лист 6, записи К-4–К-7).

| Изм. | Кол.уч | Лист | № док. | Подп. | Дата |
|---|---|---|---|---|---|
| Разраб. | | Кырлан А.С. | | | 04.11.26 |
| Пров. | | | | | |
| ГИП | | | | | |
| Н. контр. | | | | | |
| Утв. | | | | | |

**ГД-2026-006-АИ**

Квартира 58 м²

Общая площадь 55,23* м² · * размеры приняты, не замерены (реестр — л. 6, 7, К-5)

Дизайн-проект интерьера

| Стадия | Лист | Листов |
|---|---|---|
| РП | 24 | 87 |

**Однолинейная схема щита**

М б/м


**Кырлан Александр Сергеевич**

выпуск 04.11.2026 № 3da8f16a26 · стр. 27 из 96

# План принципиальных трасс

Силовые трассы и объёмы электромонтажа, слаботочка в объёмах · размеры в мм

**ПРЕДВАРИТЕЛЬНО · не для производства работ · открыто пунктов: 10 (реестр — л. 6, 7)**

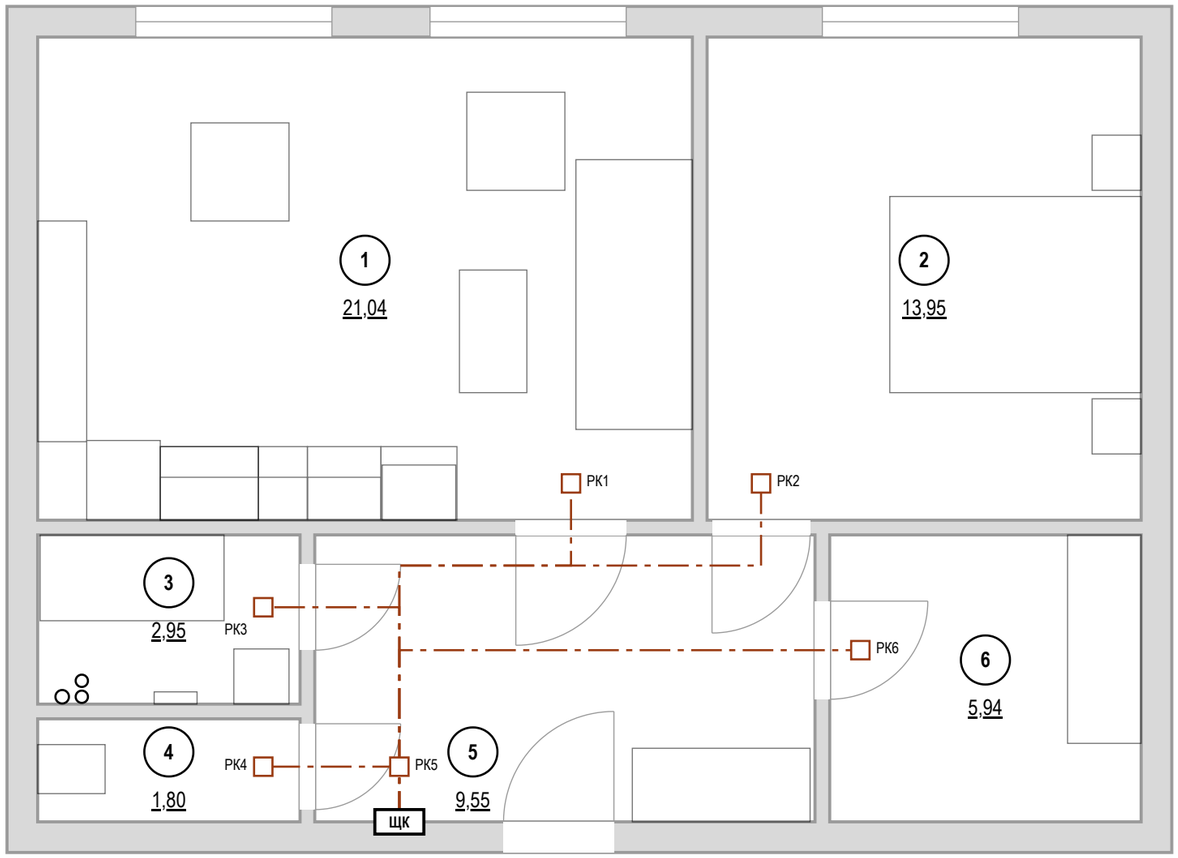


**Допущения и предложения на листе**

Основа листа: размеры сняты с плана заказчика, контрольный обмер не выполнен (К-5); высота потолка 2700 мм принята: на плане заказчика не указана (К-5); подрайон климата не задан — принят не северный (жилые от 2,5 м) (К-4); толщины стен приняты: наружные 250 мм, перегородки 120 мм — не обмерены (К-5); разрешённая мощность 15 кВт принята по типовой квартире, технических условий нет (К-6).

Знак «**» — предложение проектировщика, заказчиком не утверждено (согласовать с заказчиком): ЩС — щит слаботочный: место и состав.

См. лист открытых вопросов (лист 6, записи К-4–К-6).

## Примечания

1. За отметку 0,000 принят уровень чистого пола. Высоты Н — от чистого пола до оси изделия; привязки — от чистовой грани стены до оси механизма (у рамки на несколько постов — до оси рамки).
2. Розеточные и мокрые линии — через УЗО или дифавтомат с током утечки не более 30 мА (ПУЭ 7.1.79); в санузле выполнить ДСУП (ПУЭ 7.1.87–7.1.88).
3. Кабель — медный, исполнение нг(А)-LS (ГОСТ 31565-2012); скрытая прокладка только горизонтально и вертикально, фактические трассы зафиксировать исполнительной схемой до закрытия отделкой.
4. Расчёт нагрузок, токов КЗ, селективности и сечений — по проекту ЭОМ организации с допуском СРО; лист задаёт состав, расположение и группы.
5. Длины — по плану: от щита вверх в потолочное пространство, по дверям и коридору без захода в мокрые помещения к распределительной коробке над дверью, далее к точкам; вертикали считаются вниз и обратно (у последней точки цепочки — в один конец); запас 10 %. Трассы принципиальные: фактическую зафиксировать исполнительной схемой до закрытия отделкой.
6. Несущие стены не определены: штробы в стенах не выполнять. Маршрут проложен без штроб: горизонтали — за потолком в гофре (72,6 м) и в кабель-канале плинтуса (54,6 м), вертикали — в коробе или накладном канале (77,8 м кабеля). Точек: за потолком — 9, спуск из потолка — 7, по плинтусу — 11, плинтус и подъём — 18.
7. Вариант со штробами — работа после технического заключения: 58,99 м вертикальных штроб от потолка до каждой настенной точки; условие — только после технического заключения: стена не несущая (или вертикальная штроба в несущей согласована конструктором), глубина и ширина 20–25 мм, не в зонах 0–2 ванной. Без заключения и согласования конструктора в смету и в график эта работа не входит.
8. Слаботочные сети: кабели и точки считаются по лучам от ЩС** (лист слаботочных сетей): 50 м, портов патч-панели и коммутатора не менее 2. Изделия — в ведомости изделий.

1000 мм · печать 1:1

### Кабель по группам ВВГнг(А)-LS, м

| Гр. | мм² | Трасса | Данные |
|---|---|---|---|
| 1 | 3×1,5 | 105,4 | |
| 2 | 3×2,5 | 20,8 | |
| 3 | 3×6 | 10,7 | |

| Гр. | мм² | Трасса | Данные |
|---|---|---|---|
| 4 | 3×2,5 | 48,1 | |
| 5 | 3×2,5 | 12 | |
| 6 | 3×2,5 | 11 | |
| **Σ** | | **208** | |

### Экспликация помещений

| № | Помещение | Площадь, м² |
|---|---|---|
| 1 | Кухня-гостиная | 21,04 |
| 2 | Спальня | 13,95 |
| 3 | Ванная | 2,95 |
| 4 | Санузел | 1,80 |
| 5 | Прихожая | 9,55 |
| 6 | Гардеробная | 5,94 |
| | Итого (общая площадь) | 55,23 |

### Объёмы прокладки

| Работа, материал | Ед. | Кол. |
|---|---|---|
| Гофротруба Ø20 в потолочном пространстве | м | 72,6 |
| Кабель-канал плинтуса для силовых линий | м | 54,6 |
| Короб или накладной канал для вертикальных спусков и подъёмов | м | 44,2 |
| Коробка распределительная (РК) над дверью помещения | шт | 6 |
| Слаботочка: кабель домофона | м | 3,4 |
| Слаботочка: Кабель коаксиальный RG-6 (75 Ом) к розеткам ТВ | м | 16,3 |
| Слаботочка: Кабель U/UTP кат. 5е (LAN, Wi-Fi и камеры по PoE) | м | 30,1 |
| Слаботочка: гофротруба Ø20 отдельно от силовых | м | 44,8 |

### Штробы — только после заключения

| Работа | Ед. | Кол. |
|---|---|---|
| Вертикальные штробы 20×20 мм от потолка до каждой настенной точки (в маршрут без штроб не входят) | м | 58,99 |

### Условные обозначения

- **ЩК** — щит квартирный
- РК — распределительная коробка над дверью помещения
- магистраль от щита к РК: потолочное пространство, гофра
- мебель и сантехприборы — подложка


| Изм. | Кол.уч | Лист | № док. | Подп. | Дата | | | | |
|---|---|---|---|---|---|---|---|---|---|
| Разраб. | | Кырлан А.С. | | | 04.11.26 | **ГД-2026-006-АИ** | | | |
| Пров. | | | | | | Квартира 58 м² | | | |
| ГИП | | | | | | Общая площадь 55,23* м² · * размеры приняты, не замерены (реестр — л. 6, 7, К-5) | | | |
| | | | | | | Дизайн-проект интерьера | Стадия | Лист | Листов |
| Н. контр. | | | | | | | РП | 25 | 87 |
| Утв. | | | | | | **План принципиальных трасс** М 1:50 | **Кырлан Александр Сергеевич** | | |

выпуск 04.11.2026 № 3da8f16a26 · стр. 28 из 96

# План слаботочных сетей

Интернет, ТВ, домофон · размеры в мм · высоты от чистого пола

**ПРЕДВАРИТЕЛЬНО · не для производства работ · открыто пунктов: 10 (реестр — л. 6, 7)**

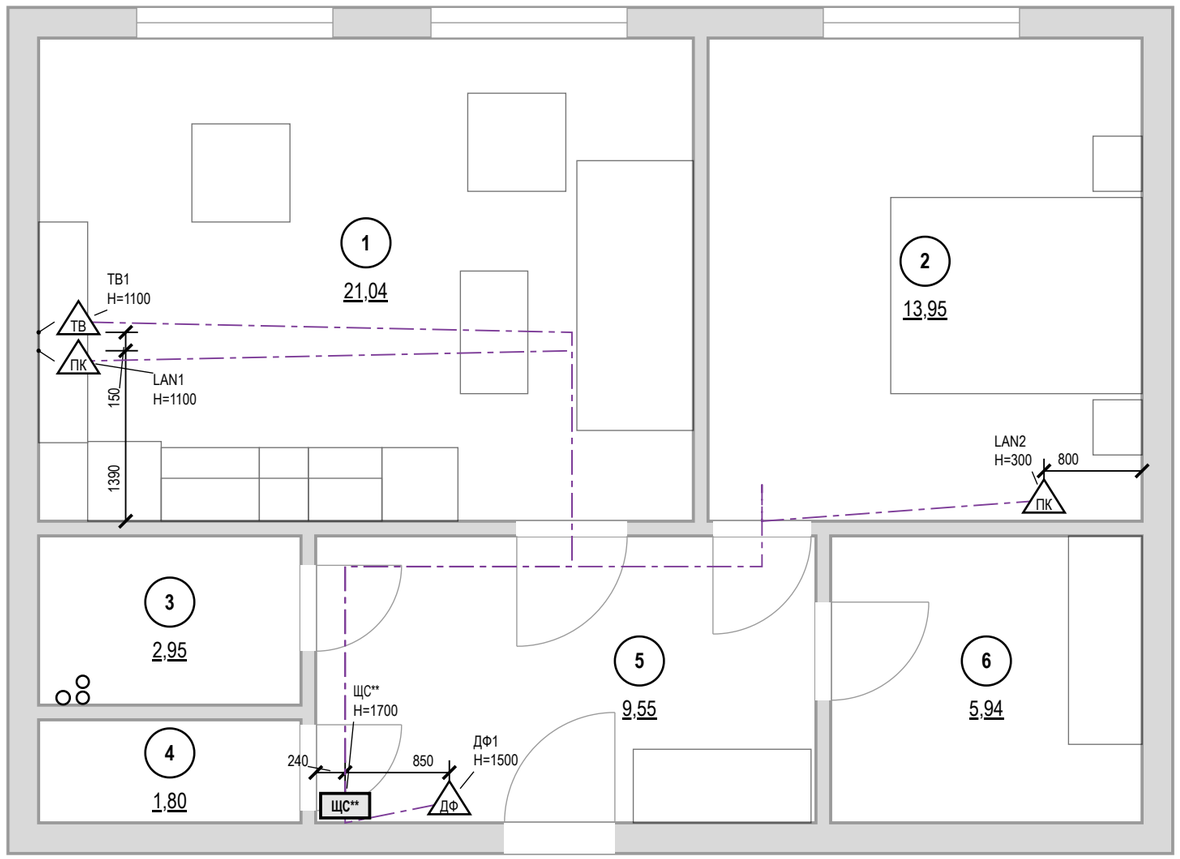


## Ведомость слаботочных точек

| Марка | Пом. | Назначение | H, мм | Кабель |
|---|---|---|---|---|
| ТВ1 | 1 | розетка ТВ | 1100 | RG-6 (75 Ом) |
| LAN1 | 1 | розетка LAN (RJ45) | 1100 | U/UTP кат. 5e/6 |
| LAN2 | 2 | розетка LAN (RJ45) | 300 | U/UTP кат. 5e/6 |
| ЩС** | 5 | щит слаботочный | 1700 | ввод пров. |
| ДФ1 | 5 | домофон (трубка) | 1500 | по системе |

## Условные обозначения

- **ЩС** — щит слаботочный: ввод провайдера, роутер, коммутатор
- ПК — розетка компьютерная RJ45
- ТВ — розетка телевизионная
- ДФ — трубка или монитор домофона
- кабель от ЩС до точки, отдельным лучом
- мебель и сантехприборы — подложка
- стояк: К1 — канализация, В1 — ХВС, Т3 — ГВС
- 1 — номер помещения, площадь м²

**Допущения и предложения на листе**

Основа листа: размеры сняты с плана заказчика, контрольный обмер не выполнен (К-5); высота потолка 2700 мм принята: на плане заказчика не указана (К-5); подрайон климата не задан — принят не северный (жилые от 2,5 м) (К-4); толщины стен приняты: наружные 250 мм, перегородки 120 мм — не обмерены (К-5); разрешённая мощность 15 кВт принята по типовой квартире, технических условий нет (К-6).

Знак «**» — предложение проектировщика, заказчиком не утверждено (согласовать с заказчиком): ЩС — щит слаботочный: место и состав.

См. лист открытых вопросов (лист 6, записи К-4–К-6).

## Примечания

1. За отметку 0,000 принят уровень чистого пола. Высоты H — от чистого пола до оси изделия; привязки — от чистовой грани стены до оси механизма (у рамки на несколько постов — до оси рамки).
2. Высота установки, не указанная на плане: розетки LAN и ТВ — 300 мм от чистого пола.
3. Слаботочные кабели — отдельно от силовых: в своей трубе или лотке, при параллельной прокладке не ближе 100 мм к силовым, пересечения под прямым углом; каждую точку — отдельным кабелем от ЩС** без скруток.
4. Трассы на листе — принципиальные; фактические зафиксировать исполнительной схемой до закрытия отделкой. Силовые линии, УЗО 30 мА, ДСУП, кабель нг(A)-LS — по листам розеток и щита.
5. Проект силовой части и расчёт токов КЗ — по проекту ЭОМ; слаботочная часть согласуется с провайдером и управляющей компанией (домофон, коллективное ТВ).

1000 мм · печать 1:1

| Изм. | Кол.уч | Лист | № док. | Подп. | Дата |
|---|---|---|---|---|---|
| Разраб. | | Кырлан А.С. | | | 04.11.26 |
| Пров. | | | | | |
| ГИП | | | | | |
| | | | | | |
| Н. контр. | | | | | |
| Утв. | | | | | |

**ГД-2026-006-АИ**

Квартира 58 м²

Общая площадь 55,23* м² · * размеры приняты, не замерены (реестр — л. 6, 7, К-5)

Дизайн-проект интерьера

| Стадия | Лист | Листов |
|---|---|---|
| РП | 26 | 87 |

**План слаботочных сетей**

М 1:50

**Кырлан Александр Сергеевич**

выпуск 04.11.2026 № 3da8f16a26 · стр. 29 из 96

04

# Отопление и вентиляция

Кырлан Александр Сергеевич


выпуск 04.11.2026 · 3da8f16a26 · стр. 30 из 96

# План вентиляции

Вытяжка, приток, переток, кондиционеры · размеры в мм · высоты от чистого пола

**ПРЕДВАРИТЕЛЬНО · не для производства работ · открыто пунктов: 10 (реестр — л. 6, 7)**

Допущения и предложения на листе. Основа листа: размеры сняты с плана заказчика, контрольный обмер не выполнен (К-5); высота потолка 2700 мм принята: на плане заказчика не указана (К-5); подрайон климата не задан — принят не северный (жилые от 2,5 м) (К-4); толщины стен приняты: наружные 250 мм, перегородки 120 мм — не обмерены (К-5); разрешённая мощность 15 кВт принята по типовой квартире, технических условий нет (К-6). Знак «*» — принято, не замерено и не подтверждено (замерить на объекте): КВ-2 — длина петли принята по типовому минимуму 3 м; паспорта выбранной модели нет. Знак «**» — предложение проектировщика, заказчиком не утверждено (согласовать с заказчиком): ИЗ-3: КВ-1 — длина петли принята по типовому минимуму 3 м; паспорта выбранной модели нет Внутренний блок перенесён со стены А (offset 3300…4200 — внутри оконного проёма 3200…4800) на стену Г, offset 300…1200 (простенок у окна 1, поток вдоль помещения к дивану); наружный блок КН-1 — в простенок между окнами (стена А, 2400…3200). См. лист открытых вопросов (лист 6, записи К-1, К-4–К-6; лист 7, запись ИЗ-3); по листу — К-1, ИЗ-3.

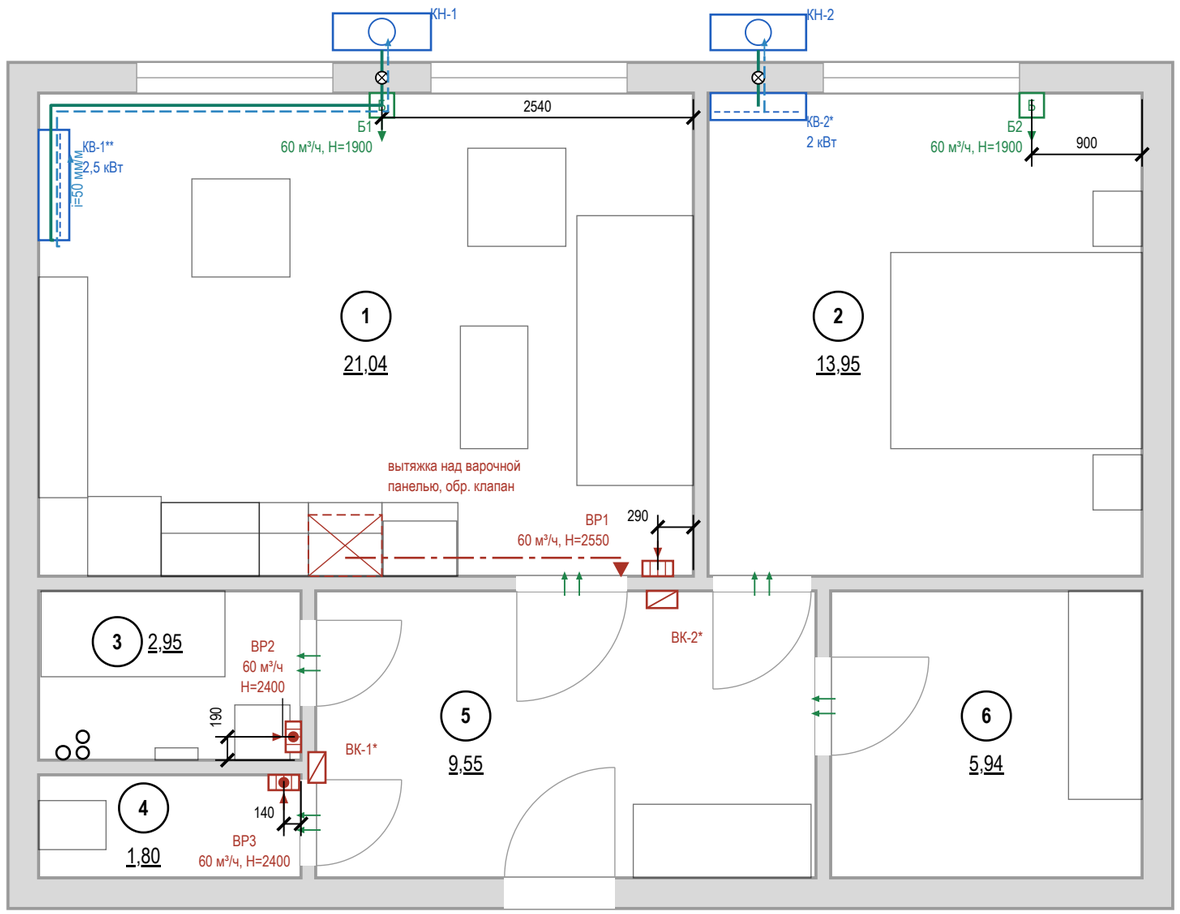


## Условные обозначения

- стояк: К1 — канализация, В1 — ХВС, Т3 — ГВС
- номер помещения, площадь м²
- вытяжная решётка в вентканал: марка, расход м³/ч, Н центра от чистого пола
- вытяжная решётка с бытовым вентилятором и обратным клапаном: марка, расход, Н
- бризер (приток с фильтром и подогревом)
- переток: зазор под полотном или переточная решётка
- кухонная вытяжка над варочной панелью
- вентканал ВК-N; «*» — принят до обмера
- воздуховод кухонной вытяжки в коробе под потолком
- отдельный вход воздуховода в вентканал, обратный клапан
- внутренний блок кондиционера (КВ-N)
- наружный блок (КН-N) на фасаде / в корзине
- трасса фреонопровода и межблочного кабеля
- дренаж конденсата (уклон стрелкой)
- отверстие в наружной стене под трассу

## Воздухообмен, м³/ч

| № | Помещение | Выт. норма | Выт. проект | Прит. норма | Прит. проект | Устрой-ства |
|---|---|---|---|---|---|---|
| 1 | Кухня-гостиная | 60 | 60 | 60 | 60 | ВР1, Б1 |
| 2 | Спальня | | | 60 | 60 | Б2 |
| 3 | Ванная | 50 | 60 | | | ВР2 |
| 4 | Санузел | 25 | 60 | | | ВР3 |
| 6 | Гардеробная | 3 | | | | переток |
| | **Итого** | **138** | **180** | **120** | **120** | |
| | Норма по жильцам: 30×2 | | | 60 | | |

Воздухообмен квартиры — по большей из сумм притока и вытяжки: норма 138 м³/ч, проект 180 м³/ч.
Вытяжка не меньше притока — баланс сведён.

## Кондиционеры

| Марка | Помещение | Нар. блок | Трасса, м | Дренаж |
|---|---|---|---|---|
| КВ-1** | 1. Кухня-гостиная | КН-1 | 3,0 | наружу, i=50 мм/м |
| КВ-2* | 2. Спальня | КН-2 | 3,0 п | наружу, i=50 мм/м |

## Примечания

1. Расчёт систем ОВ и подбор оборудования — проектная организация с допуском СРО; лист даёт места, трассы и привязки.
2. Нормы вытяжки — СП 54.13330.2022 (Изм. 1, 2), табл. 7.1: кухня с электроплитой 60 м³/ч, с газовой 100; ванная и совмещённый санузел 50; уборная 25; гардеробная 0,2 ч⁻¹. Приток в жилые — 3 м³/ч на 1 м² (менее 20 м² общей площади на человека), иначе 30 м³/ч на человека.
3. Вентканалы и шахты не сужать, не переносить и не закрывать; вентилятор и кухонная вытяжка — через обратный клапан, без перекрытия естественной тяги.
4. Кухонная вытяжка в воздухообмен не включена: воздуховод не менее Ø125 в коробе, вход в канал отдельный.
5. Переток — зазор под полотнами межкомнатных дверей или переточная решётка.
6. Дренаж кондиционера — непрерывный уклон 40–60 мм/м без контруклонов (СТО НОСТРОЙ 2.23.1-2011, п. 5.8.4); врезка в К1 — через сифон (п. 5.8.9); длина трассы и перепад высот — по паспорту блока; внутренний блок — не ближе 150 мм к потолку, не над кроватью и рабочим местом.
7. Наружный блок на фасаде многоквартирного дома — с согласия собственников (общее имущество); при наличии корзин — только в них.
8. «п» в графе «Трасса» — трасса фреона по плану короче минимума, разница выбрана компенсационной петлёй (бухтой): КВ-2* — по плану 0,8 м, с петлёй 3,0 м. Длина петли принята по минимуму трассы (3,0 м) и зависит от паспорта модели кондиционера, которая ещё не выбрана: минимум и максимум трассы — типовые, по паспорту модели, до заказа сверить и при необходимости изменить петлю или место наружного блока. Бухту уложить в коробе или за внутренним блоком, не в штробе.
9. Привязки оборудования — по паспортам приобретённых моделей, до черновых работ.
10. Привязки — до обмера: вентканалы ВК-N* приняты проектировщиком, решётки и воздуховоды — от них. До черновых работ — обмер каналов и тяги, лист перевыпустить по факту.

1000 мм · печать 1:1

| Изм. | Кол.уч | Лист | № док. | Подп. | Дата |
|---|---|---|---|---|---|
| Разраб. | | Кырлан А.С. | | | 04.11.26 |
| Пров. | | | | | |
| ГИП | | | | | |
| | | | | | |
| Н. контр. | | | | | |
| Утв. | | | | | |

**ГД-2026-006-АИ**

Квартира 58 м²

Общая площадь 55,23* м² · * размеры приняты, не замерены (реестр — л. 6, 7, К-5)

Дизайн-проект интерьера

| Стадия | Лист | Листов |
|---|---|---|
| РП | 27 | 87 |

**План вентиляции**

М 1:50


**Кырлан Александр Сергеевич**

выпуск 04.11.2026 № 3da8f16a26 · стр. 31 из 96

# План отопления

Радиаторы, стояки, подводки · размеры в мм · высоты от чистого пола

**ПРЕДВАРИТЕЛЬНО · не для производства работ · открыто пунктов: 10 (реестр — л. 6, 7)**

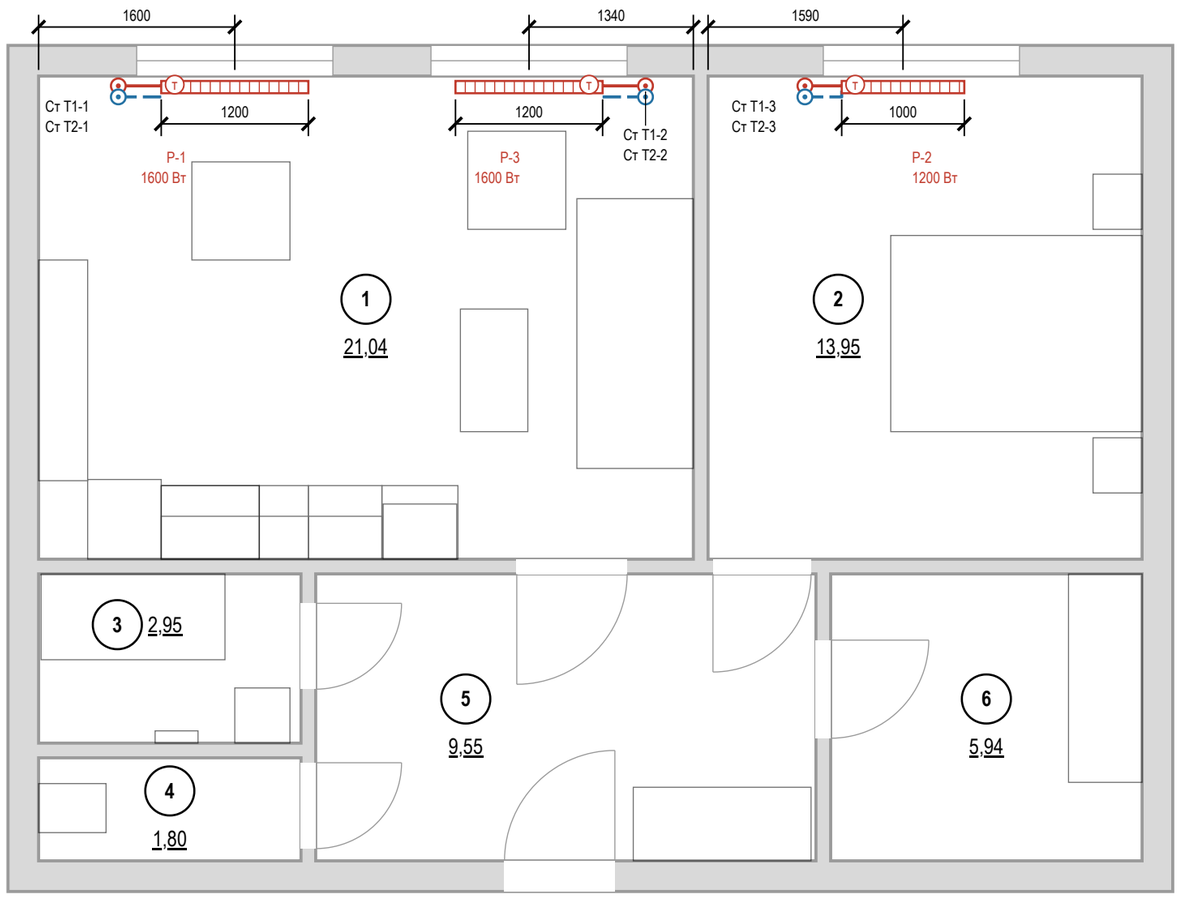


## Условные обозначения

- 1 — номер помещения, площадь м²
- радиатор отопления (марка РО-N, длина по плану)
- Т — клапан с термоголовкой на подаче
- стояк отопления, подающий (Ст Т1-N)
- стояк отопления, обратный (Ст Т2-N)
- Т1 — отопление, подающий трубопровод
- Т2 — отопление, обратный трубопровод

## Ведомость радиаторов

| Марка | Помещение | Тип | Д×В×Г, мм | Низ / стена | Q, Вт |
|---|---|---|---|---|---|
| Р-1 | 1. Кухня-гостиная | панельный 22 | 1200×500×100 | 120 / 40 | 1600 |
| Р-3 | 1. Кухня-гостиная | панельный 22 | 1200×500×100 | 120 / 40 | 1600 |
| Р-2 | 2. Спальня | панельный 22 | 1000×500×100 | 120 / 40 | 1200 |

Низ — от чистого пола, стена — зазор до задней панели, мм.

**Привязки — до обмера**

Стояки отопления в исходных данных не заданы: показаны у откосов окон, подводки — принципиально. До черновых работ — обмер стояков и паспорта приборов; лист перевыпустить по факту.

## Примечания

1. Расчёт системы отопления, теплопотерь и подбор приборов — проектная организация с допуском СРО; лист даёт места и привязки.
2. Тип, длина и мощность радиаторов — по теплотехническому расчёту; лист задаёт места, зазоры и подключение.
3. Зазоры радиатора: низ не менее 100 мм от чистого пола, верх не менее 100 мм до подоконника, 30–50 мм от стены до задней панели; центр по оси окна с допуском ±20 мм. Верх до подоконника — 180 мм.
4. Радиаторы не закрывать глухими коробами и мебелью; перенос и замена приборов в многоквартирном доме — переустройство, согласование с управляющей организацией (ЖК РФ ст. 25–26); вынос на лоджию запрещён.
5. Трубы отопления через межквартирные стены не прокладывать (СП 51.13330.2011, п. 9.19); через перекрытия и перегородки — в гильзах.
6. Привязки приборов и подводок — по паспортам приобретённых радиаторов и клапанов, до черновых работ.
7. До закрытия отделкой трубопроводы отопления испытать гидростатическим давлением с оформлением акта (СП 73.13330.2016, 7.2–7.3).

**Допущения и предложения на листе**

Основа листа: размеры сняты с плана заказчика, контрольный обмер не выполнен (К-5); высота потолка 2700 мм принята: на плане заказчика не указана (К-5); подрайон климата не задан — принят не северный (жилые от 2,5 м) (К-4); толщины стен приняты: наружные 250 мм, перегородки 120 мм — не обмерены (К-5); разрешённая мощность 15 кВт принята по типовой квартире, технических условий нет (К-6).

См. лист открытых вопросов (лист 6, записи К-4–К-6).

1000 мм · печать 1:1

| Изм. | Кол.уч | Лист | № док. | Подп. | Дата |
|---|---|---|---|---|---|
| Разраб. | | Кырлан А.С. | | | 04.11.26 |
| Пров. | | | | | |
| ГИП | | | | | |
| Н. контр. | | | | | |
| Утв. | | | | | |

**ГД-2026-006-АИ**

Квартира 58 м²

Общая площадь 55,23* м² · * размеры приняты, не замерены (реестр — л. 6, 7, К-5)

Дизайн-проект интерьера

| Стадия | Лист | Листов |
|---|---|---|
| РП | 28 | 87 |

**План отопления**

М 1:50

**Кырлан Александр Сергеевич**

выпуск 04.11.2026 № 3da8f16a26 · стр. 32 из 96

05

# Водоснабжение и канализация

Кырлан Александр Сергеевич


выпуск 04.11.2026 · 3da8f16a26 · стр. 33 из 96

# План выводов сантехники


Выводы В1, Т3, К1 · привязки от чистовых стен · высоты от чистого пола, мм

ПРЕДВАРИТЕЛЬНО · не для производства работ · открыто пунктов: 10 (реестр — л. 6, 7)


### Фрагмент 1. Кухня-гостиная (пом. 1)

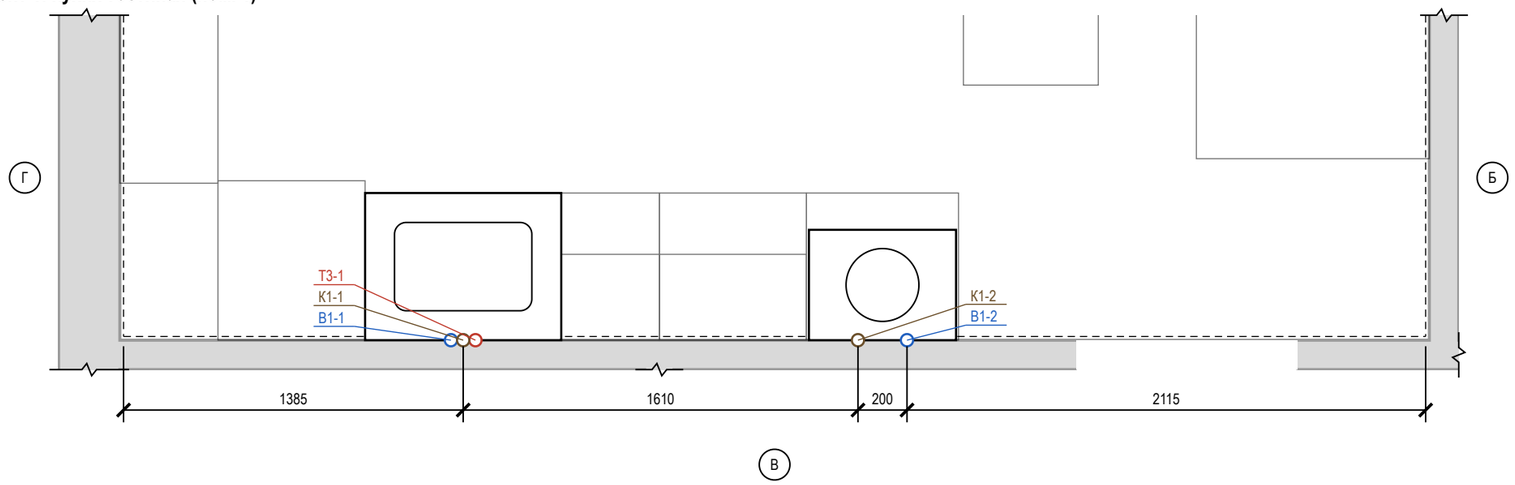


### Фрагмент 2. Ванная (пом. 3)

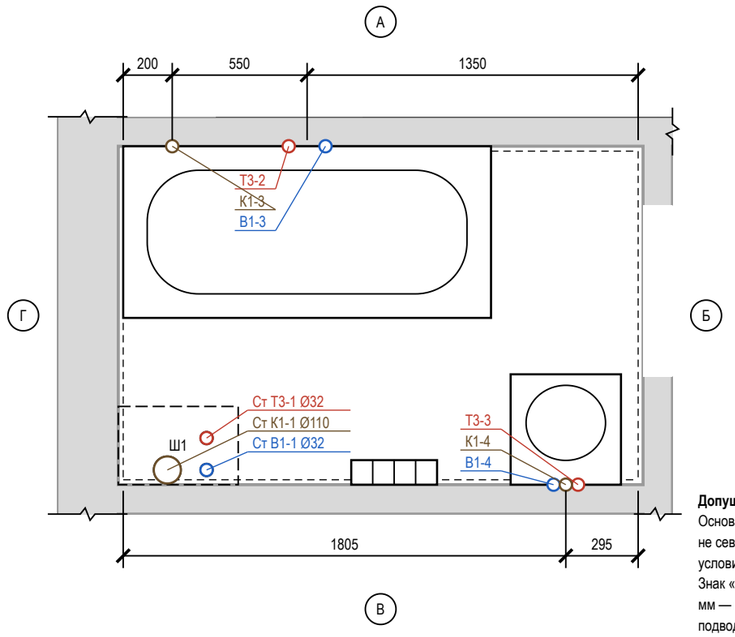


### Фрагмент 3. Санузел (пом. 4)

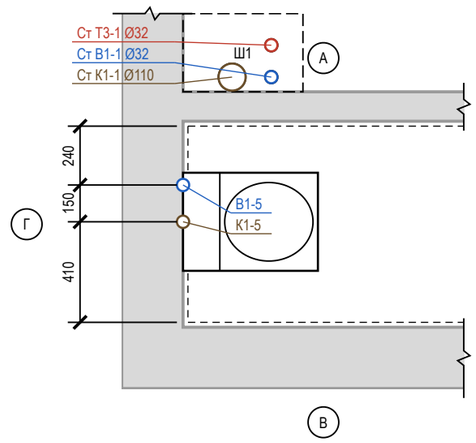


### Ведомость привязок выводов

| Код | Прибор | Ø | Н, мм | Привязка от чист. стен, мм | Прим. |
|---|---|---|---|---|---|
| В1-1 | П4 мойка кухонная | ½" | 550 | ст. В: 1335 от Г | межос. 100 |
| Т3-1 | П4 мойка кухонная | ½" | 550 | ст. В: 1435 от Г | межос. 100 |
| К1-1 | П4 мойка кухонная | Ø50 | 400 | ст. В: 1385 от Г | |
| В1-2 | П6** стиральная машина | ½" | 600 | ст. В: 2115 от Б | кран машины |
| К1-2 | П6** стиральная машина | Ø40 | 600 | ст. В: 2315 от Б | |
| В1-3 | П1** ванна | ½" | 800 | ст. А: 825 от Г | межос. 150 |
| Т3-2 | П1** ванна | ½" | 800 | ст. А: 675 от Г | межос. 150 |
| К1-3 | П1** ванна | Ø50 | 50 | ст. А: 200 от Г | |
| В1-4 | П3** умывальник | ½" | 550 | ст. В: 345 от Б | межос. 100 |
| Т3-3 | П3** умывальник | ½" | 550 | ст. В: 245 от Б | межос. 100 |
| К1-4 | П3** умывальник | Ø50 | 500 | ст. В: 295 от Б | |
| В1-5 | П20 унитаз подвесной | ½" | 150 | ст. Г: 240 от А | в раме инсталляции |
| К1-5 | П20 унитаз подвесной | Ø110 | 230 | ст. Г: 390 от А | |

* — высота по практике монтажа; сверить по паспорту прибора

### Условные обозначения

- вывод В1 (код — в ведомости привязок)
- вывод Т3 (код — в ведомости привязок)
- вывод К1 (код — в ведомости привязок)
- сантехприбор по расстановке (габарит модели)
- чистовая поверхность стены (от неё привязки)
- стояк «Ст К1-N / Ст В1-N» (ГОСТ 21.601), Ø мм
- шахта / короб стояков, люк 300×400
- линия обрыва (граница фрагмента)
- А — обозначение стены А–Г (как на развёртках)

**Допущения и предложения на листе**

Основа листа: размеры сняты с плана заказчика, контрольный обмер не выполнен (К-5); высота потолка 2700 мм принята: на плане заказчика не указана (К-5); подрайон климата не задан — принят не северный (жилые от 2,5 м) (К-4); толщины стен приняты: наружные 250 мм, перегородки 120 мм — не обмерены (К-5); разрешённая мощность 15 кВт принята по типовой квартире, технических условий нет (К-6).

Знак «**» — предложение проектировщика, заказчиком не утверждено (согласовать с заказчиком): К-2: П1 — ванна 1500 вместо 1600 — не заходит в проход перед проёмом Д-4; перед ванной 680 мм — глубина помещения; П3 — умывальник у стены В справа от ванны — перед ним свободно 750 мм, до стены Б 90 мм; К-7: П6 — стиральная машина на кухне: в ванной и санузле места нет; подвод ХВС с шаровым краном, слив — встраиваемый сифон с обратным клапаном (водяной затвор), отдельная группа 6 щита с УЗО 30 мА.

Открытые вопросы и конфликты по листу: К-2, К-7.

См. лист открытых вопросов (лист 6, записи К-2, К-4–К-7).

### Примечания

1. Привязки выводов даны от чистовых поверхностей стен (облицовка на сторону: кухня-гостиная — 15 мм (по данным); ванная — 20 мм (по данным); санузел — 20 мм (по данным)); эти же грани — на развёртках и в раскладке плитки. Высоты — от чистого пола помещения.
2. Высоты и межосевые, отмеченные «*», приняты по практике монтажа; до черновой разводки сверить по паспорту выбранного прибора (смеситель, инсталляция, сифон).
3. Горячая вода (Т3) — слева от холодной (В1), если смотреть на прибор. Допуск установки выводов: ±5 мм в группе, ±20 мм у отдельно стоящих.
4. Расчёт систем водоснабжения и канализации и подбор оборудования выполняет проектная организация; лист задаёт места и высоты выводов.
5. Стояки в коробах/шахтах Ш1 не замоноличивать; стояк К1 в коробе — звукоизоляция стояка в коробе без жёсткого контакта с трубой; к арматуре и ревизиям — люк не меньше 300×400.

1000 мм · печать 1:1

| Изм. | Кол.уч | Лист | № док. | Подп. | Дата |
|---|---|---|---|---|---|
| Разраб. | | Кырлан А.С. | | | 04.11.26 |
| Пров. | | | | | |
| ГИП | | | | | |
| | | | | | |
| Н. контр. | | | | | |
| Утв. | | | | | |

**ГД-2026-006-АИ**

Квартира 58 м²

Общая площадь 55,23* м² · * размеры приняты, не замерены (реестр — л. 6, 7, К-5)

Дизайн-проект интерьера

| Стадия | Лист | Листов |
|---|---|---|
| РП | 29 | 87 |

**План выводов сантехники**

М 1:25

**Кырлан Александр Сергеевич**


выпуск 04.11.2026 № 3da8f16a26 · стр. 34 из 96

# Схема разводки водопровода и канализации


Схемы систем В1, Т3, К1 · трассы принципиальные · уклоны в мм на 1 м · план М 1:200, фрагменты М 1:25

**ПРЕДВАРИТЕЛЬНО · не для производства работ · открыто пунктов: 10 (реестр — л. 6, 7)**


## План квартиры (М 1:200)

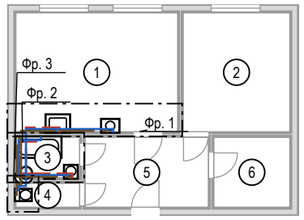



## Фр. 1. Кухня-гостиная (М 1:25)

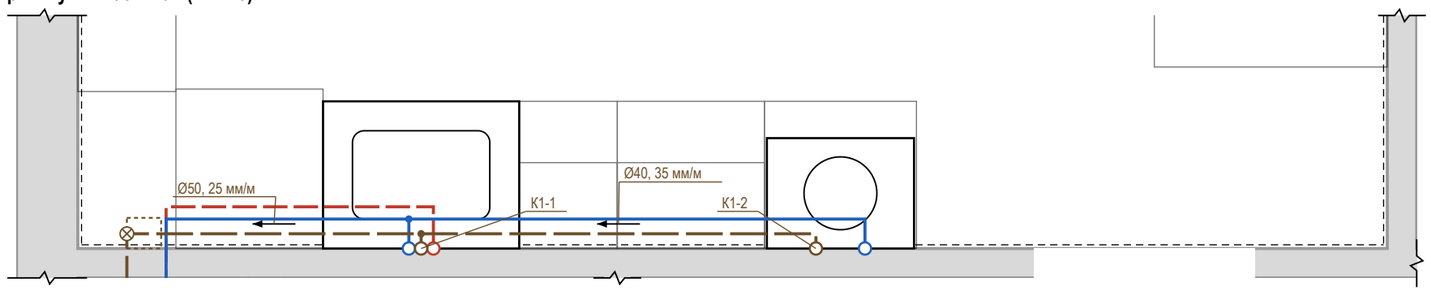


## Фр. 2. Ванная (М 1:25)

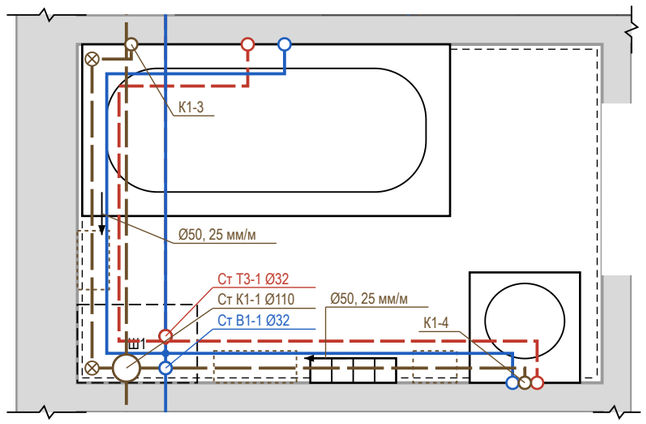


## Фр. 3. Санузел (М 1:25)

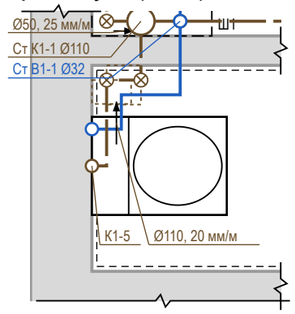


## Условные обозначения

- В1 — водопровод хозяйственно-питьевой (ХВС), PP-R Ø20
- Т3 — горячее водоснабжение, подача (ГВС), PP-R Ø20
- К1 — канализация бытовая
- направление уклона К1 / пола: Ø, мм на 1 м
- ревизия (прочистка) К1 — доступ сохранить
- тройник (ответвление к прибору)
- короб К1 над чистым полом (ГКЛВ под плитку)
- вывод В1 (код — в ведомости привязок)
- вывод Т3 (код — в ведомости привязок)
- вывод К1 (код — в ведомости привязок)
- сантехприбор по расстановке (габарит модели)
- стояк «Ст К1-N / Ст В1-N» (ГОСТ 21.601), Ø мм
- шахта / короб стояков, люк 300×400
- линия обрыва (граница фрагмента)
- граница фрагмента на плане (Фр. N)

## Профиль выпусков К1 (до врезки в стояк)

| Выпуск | Прибор | Ø | L, м | i, мм/м | Δh, мм | Прокладка, мм |
|---|---|---|---|---|---|---|
| К1-5 | П20 унитаз подвесной | Ø110 | 0,79 | 20 | 16 | короб 160×140 |
| К1-1 | П4 мойка кухонная | Ø50 | 2,76 | 25 | 69 | короб 150×110 |
| К1-4 | П3** умывальник | Ø50 | 1,69 | 25 | 42 | короб 130×110 |
| К1-3 | П1** ванна | Ø50 | 1,62 | 25 | 41 | короб 130×110 |
| К1-2 | П6** стиральная машина | Ø40 | 4,37 | 35 | 153 | короб 230×110 |

Короб h×b: h — от чистого пола, b — от чистовой стены. Стяжка 90 мм — лист полов.

## Узел ввода В1, Т3 (схема, без масштаба)




состав узла — по согласованию

⊗ Ст К1-1: ревизия на стояке — люк в коробе

## Примечания

1. Трассы принципиальные, построены от стояков вдоль стен помещений; фактическое положение фиксируется исполнительной схемой с привязками (фото с рулеткой) до закрытия.
2. Уклон К1 не менее 1/d и не более 150 мм/м (СП 30.13330.2020, п. 19.1), приняты практические уклоны; поворот — двумя отводами 45°, ревизия после поворота, доступ сохранить. Стояк К1 в коробе — звукоизоляция стояка в коробе, без жёсткого контакта короба с трубой.
3. Решение по К1: стяжка 90 мм не укрывает трубы (нужно Ø + Δh + 45 мм) — выпуски идут над чистым полом вдоль стен; К1-5, К1-1, К1-4, К1-3, К1-2 — в коробе ГКЛВ под плитку (размеры в профиле). Короба — на развёртках; отметку низа врезки в стояк замерить до черновых работ.
4. Отводы К1-2 (4,4 м) длиннее 4 м без вентиляции — у прибора воздушный клапан Ø50 в доступном месте (за люком или в тумбе) либо вентилируемый отвод (EN 12056-2, табл. 4); предложение проектировщика, подбор — проектная организация.
5. Состав узла ввода В1, Т3 — по согласованию: на схеме типовой узел — кран шаровой, фильтр, счётчик, обратный клапан, кран; состав и места не определены (записи реестра нет). Доступ к арматуре — через люк не меньше 300×400. Водопровод — в штробе стен или в коробах; трубы испытать давлением до закрытия (акт скрытых работ).
6. Расчёт систем, диаметры магистралей и подбор оборудования выполняет проектная организация; врезка и перенос стояков — по согласованию с управляющей организацией. Арматуру и привязки сверить по паспортам приборов.

Допущения и предложения на листе. Знак «**» предложено (согласовать). См. лист открытых вопросов (листы 6, 7).

| Изм. | Кол.уч | Лист | № док. | Подп. | Дата |
|---|---|---|---|---|---|
| Разраб. | | Кырлан А.С. | | | 04.11.26 |
| Пров. | | | | | |
| ГИП | | | | | |
| Н. контр. | | | | | |
| Утв. | | | | | |

**ГД-2026-006-АИ**

Квартира 58 м²

Общая площадь 55,23* м² · * размеры приняты, не замерены (реестр — л. 6, 7, К-5)

Дизайн-проект интерьера

| Стадия | Лист | Листов |
|---|---|---|
| РП | 30 | 87 |

**Схема разводки водопровода и канализации**

М 1:200; 1:25


**Кырлан Александр Сергеевич**

выпуск 04.11.2026 № 3da8f16a26 · стр. 35 из 96

# Аксонометрическая схема В1 (холодное водоснабжение)

аксонометрия · диаметры, уклоны, отметки, стояки и приборы · трассы принципиальные

**Схема В1 (М 1:50; по вертикали и горизонтали один масштаб, глубина — ×0,5 под 45°)**

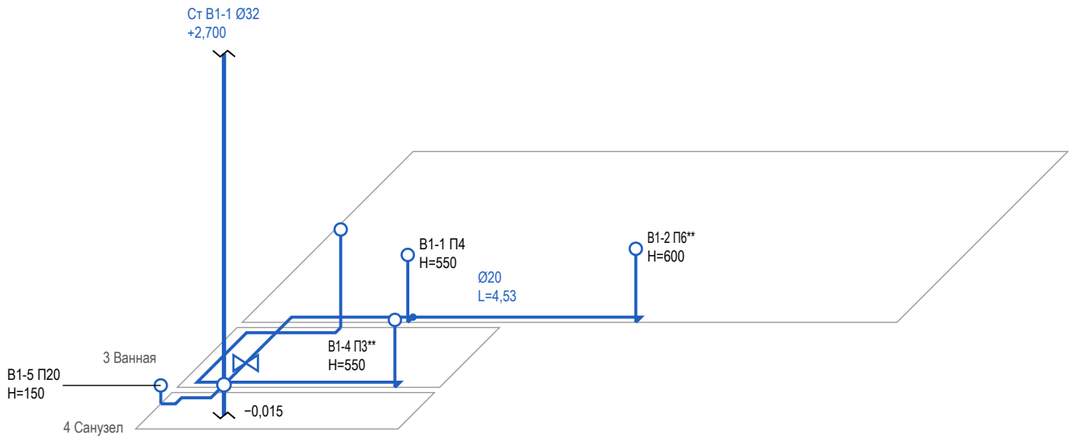


**ПРЕДВАРИТЕЛЬНО · не для производства работ · открыто пунктов: 10 (реестр — л. 6, 7)**

## Условные обозначения

- В1 — водопровод хозяйственно-питьевой (ХВС), PP-R Ø20
- вывод В1 (код — в ведомости привязок)
- стояк «Ст К1-N / Ст В1-N» (ГОСТ 21.601), Ø мм
- стояк в плане (на отметке пола); вертикаль — стояк по высоте, разрыв — перекрытие
- тройник (ответвление к прибору)
- кран шаровой

**Допущения и предложения на листе**

Основа листа: размеры сняты с плана заказчика, контрольный обмер не выполнен (К-5); высота потолка 2700 мм принята: на плане заказчика не указана (К-5); подрайон климата не задан — принят не северный (жилые от 2,5 м) (К-4); толщины стен приняты: наружные 250 мм, перегородки 120 мм — не обмерены (К-5); разрешённая мощность 15 кВт принята по типовой квартире, технических условий нет (К-6).

Знак «**» — предложение проектировщика, заказчиком не утверждено (согласовать с заказчиком): К-2: П3 — умывальник у стены В справа от ванны — перед ним свободно 750 мм, до стены Б 90 мм; К-7: П6 — стиральная машина на кухне: в ванной и санузле места нет; подвод ХВС с шаровым краном, слив — встраиваемый сифон с обратным клапаном (водяной затвор), отдельная группа 6 щита с УЗО 30 мА.

См. лист открытых вопросов (лист 6, записи К-2, К-4–К-7).

## Примечания

1. Схема В1 построена по тем же трассам, что план разводки: положение в плане сохранено, глубина — в масштабе ×0,5. Трассы принципиальные; фактическое положение фиксируется исполнительной схемой до закрытия.
2. Высоты Н — от чистого пола помещения, мм. Отметка прокладки магистрали В1 (в стяжке, в стене или по полу) в данных не задана: участки показаны на уровне пола условно (записи реестра нет).
3. Узел ввода В1 (кран, фильтр, счётчик, обратный клапан, кран) — на схеме разводки; состав узла ввода — по согласованию. Кран шаровой — на первом участке от стояка.
4. Трубы испытать давлением до закрытия (акт скрытых работ, опрессовка по СП 73.13330.2016).
5. Диаметры, высоты выводов и места кранов — по паспортам выбранных приборов и расчёту проектной организации.
6. Расчёт систем, диаметры магистралей и подбор оборудования выполняет проектная организация.

1000 мм · печать 1:1

| Изм. | Кол.уч | Лист | № док. | Подп. | Дата |
|---|---|---|---|---|---|
| Разраб. | | Кырлан А.С. | | | 04.11.26 |
| Пров. | | | | | |
| ГИП | | | | | |
| | | | | | |
| Н. контр. | | | | | |
| Утв. | | | | | |

**ГД-2026-006-АИ**

Квартира 58 м²

Общая площадь 55,23* м² · * размеры приняты, не замерены (реестр — л. 6, 7, К-5)

Дизайн-проект интерьера

| Стадия | Лист | Листов |
|---|---|---|
| РП | 31 | 87 |

**Аксонометрическая схема В1 (холодное водоснабжение)**

М 1:50


**Кырлан Александр Сергеевич**

выпуск 04.11.2026 № 3da8f16a26 · стр. 36 из 96

# Аксонометрическая схема Т3 (горячее водоснабжение)

аксонометрия · диаметры, уклоны, отметки, стояки и приборы · трассы принципиальные

**Схема Т3 (М 1:50; по вертикали и горизонтали один масштаб, глубина — ×0,5 под 45°)**

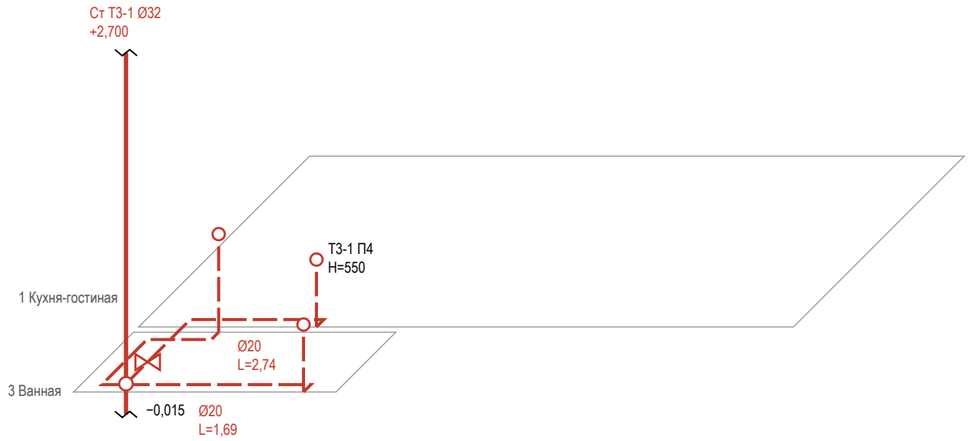


**ПРЕДВАРИТЕЛЬНО · не для производства работ · открыто пунктов: 10 (реестр — л. 6, 7)**

## Условные обозначения

- Т3 — горячее водоснабжение, подача (ГВС), PP-R Ø20
- вывод Т3 (код — в ведомости привязок)
- стояк «Ст К1-N / Ст В1-N» (ГОСТ 21.601), Ø мм
- стояк в плане (на отметке пола); вертикаль — стояк по высоте, разрыв — перекрытие
- тройник (ответвление к прибору)
- кран шаровой

**Допущения и предложения на листе**

Основа листа: размеры сняты с плана заказчика, контрольный обмер не выполнен (К-5); высота потолка 2700 мм принята: на плане заказчика не указана (К-5); подрайон климата не задан — принят не северный (жилые от 2,5 м) (К-4); толщины стен приняты: наружные 250 мм, перегородки 120 мм — не обмерены (К-5); разрешённая мощность 15 кВт принята по типовой квартире, технических условий нет (К-6).

См. лист открытых вопросов (лист 6, записи К-4–К-6).

## Примечания

1. Схема Т3 построена по тем же трассам, что план разводки: положение в плане сохранено, глубина — в масштабе ×0,5. Трассы принципиальные; фактическое положение фиксируется исполнительной схемой до закрытия.
2. Высоты Н — от чистого пола помещения, мм. Отметка прокладки магистрали Т3 (в стяжке, в стене или по полу) в данных не задана: участки показаны на уровне пола условно (записи реестра нет).
3. Узел ввода Т3 (кран, фильтр, счётчик, обратный клапан, кран) — на схеме разводки; состав узла ввода — по согласованию. Кран шаровой — на первом участке от стояка.
4. Циркуляция ГВС в данных не задана — циркуляционного трубопровода на схеме нет (записи реестра нет).
5. Трубы испытать давлением до закрытия (акт скрытых работ, опрессовка по СП 73.13330.2016).
6. Диаметры, высоты выводов и места кранов — по паспортам выбранных приборов и расчёту проектной организации.
7. Расчёт систем, диаметры магистралей и подбор оборудования выполняет проектная организация.

1000 мм · печать 1:1

| Изм. | Кол.уч | Лист | № док. | Подп. | Дата |
|---|---|---|---|---|---|
| Разраб. | | Кырлан А.С. | | | 04.11.26 |
| Пров. | | | | | |
| ГИП | | | | | |
| Н. контр. | | | | | |
| Утв. | | | | | |

**ГД-2026-006-АИ**

Квартира 58 м²

Общая площадь 55,23* м² · * размеры приняты, не замерены (реестр — л. 6, 7, К-5)

Дизайн-проект интерьера

| Стадия | Лист | Листов |
|---|---|---|
| РП | 32 | 87 |

**Аксонометрическая схема Т3 (горячее водоснабжение)**

М 1:50


**Кырлан Александр Сергеевич**

выпуск 04.11.2026 № 3da8f16a26 · стр. 37 из 96

# Аксонометрическая схема К1 (канализация)

аксонометрия · диаметры, уклоны, отметки, стояки и приборы · трассы принципиальные

**Схема К1 (М 1:50; по вертикали и горизонтали один масштаб, глубина — ×0,5 под 45°)**

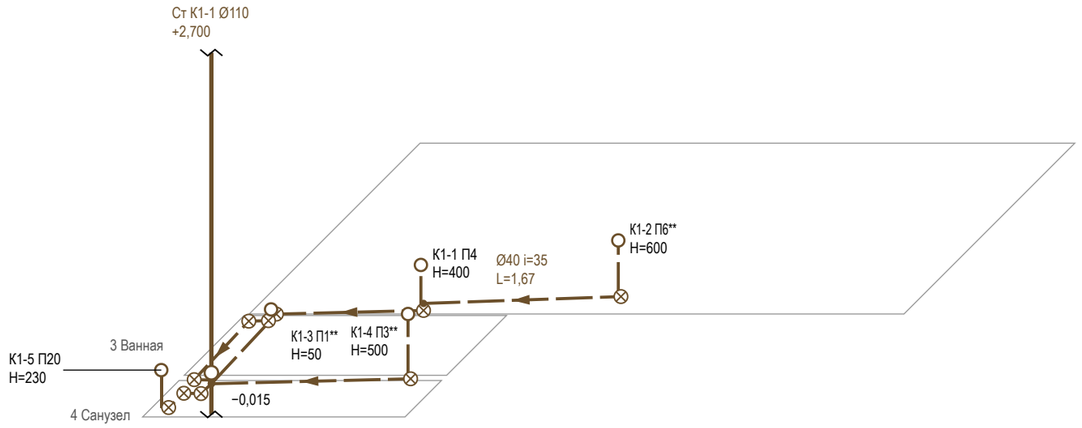


**ПРЕДВАРИТЕЛЬНО · не для производства работ · открыто пунктов: 10 (реестр — л. 6, 7)**

## Условные обозначения

- К1 — канализация бытовая
- вывод К1 (код — в ведомости привязок)
- стояк «Ст К1-N / Ст В1-N» (ГОСТ 21.601), Ø мм
- стояк в плане (на отметке пола); вертикаль — стояк по высоте, разрыв — перекрытие
- направление уклона К1 / пола: Ø, мм на 1 м
- ревизия (прочистка) К1 — доступ сохранить
- тройник (ответвление к прибору)

**Допущения и предложения на листе**

Основа листа: размеры сняты с плана заказчика, контрольный обмер не выполнен (К-5); высота потолка 2700 мм принята: на плане заказчика не указана (К-5); подрайон климата не задан — принят не северный (жилые от 2,5 м) (К-4); толщины стен приняты: наружные 250 мм, перегородки 120 мм — не обмерены (К-5); разрешённая мощность 15 кВт принята по типовой квартире, технических условий нет (К-6).

Знак «**» — предложение проектировщика, заказчиком не утверждено (согласовать с заказчиком): К-2: П1 — ванна 1500 вместо 1600 — не заходит в проход перед проёмом Д-4; перед ванной 680 мм — глубина помещения; П3 — умывальник у стены В справа от ванны — перед ним свободно 750 мм, до стены Б 90 мм; К-7: П6 — стиральная машина на кухне: в ванной и санузле места нет; подвод ХВС с шаровым краном, слив — встраиваемый сифон с обратным клапаном (водяной затвор), отдельная группа 6 щита с УЗО 30 мА.

См. лист открытых вопросов (лист 6, записи К-2, К-4–К-7).

## Примечания

1. Схема К1 построена по тем же трассам, что план разводки: положение в плане сохранено, глубина — в масштабе ×0,5. Трассы принципиальные; фактическое положение фиксируется исполнительной схемой до закрытия.
2. Отметки — от плиты перекрытия: низ трубы у врезки в стояк — отметка из данных выпуска, к прибору труба поднимается на уклон i, мм/м (уклон не менее 1/d и не более 150 мм/м, СП 30.13330.2020, п. 19.1); чистый пол — выше плиты на стяжку (высота пирога пола). Высота выпуска прибора H — от чистого пола.
3. Ревизия — на повороте и в начале участка; стояк К1 в коробе с люком — звукоизоляция стояка в коробе; поворот — двумя отводами 45°.
4. Трубы испытать давлением до закрытия (акт скрытых работ, опрессовка по СП 73.13330.2016).
5. Диаметры, высоты выводов и места кранов — по паспортам выбранных приборов и расчёту проектной организации.
6. Расчёт систем, диаметры магистралей и подбор оборудования выполняет проектная организация.

1000 мм · печать 1:1

| Изм. | Кол.уч | Лист | № док. | Подп. | Дата |
|---|---|---|---|---|---|
| Разраб. | | Кырлан А.С. | | | 04.11.26 |
| Пров. | | | | | |
| ГИП | | | | | |
| Н. контр. | | | | | |
| Утв. | | | | | |

**ГД-2026-006-АИ**

Квартира 58 м²

Общая площадь 55,23* м² · * размеры приняты, не замерены (реестр — л. 6, 7, К-5)

Дизайн-проект интерьера

| Стадия | Лист | Листов |
|---|---|---|
| РП | 33 | 87 |

**Аксонометрическая схема К1 (канализация)**

М 1:50

**Кырлан Александр Сергеевич**


выпуск 04.11.2026 № 3da8f16a26 · стр. 38 из 96

# Развёртки мокрых зон: выводы ВК. Кухня-гостиная

пом. 1 · выводы В1, Т3, К1 на стенах · высоты от чистого пола, привязки от чистовых углов, мм

ПРЕДВАРИТЕЛЬНО · не для производства работ · открыто пунктов: 10 (реестр — л. 6, 7)

## Стена В (М 1:20)

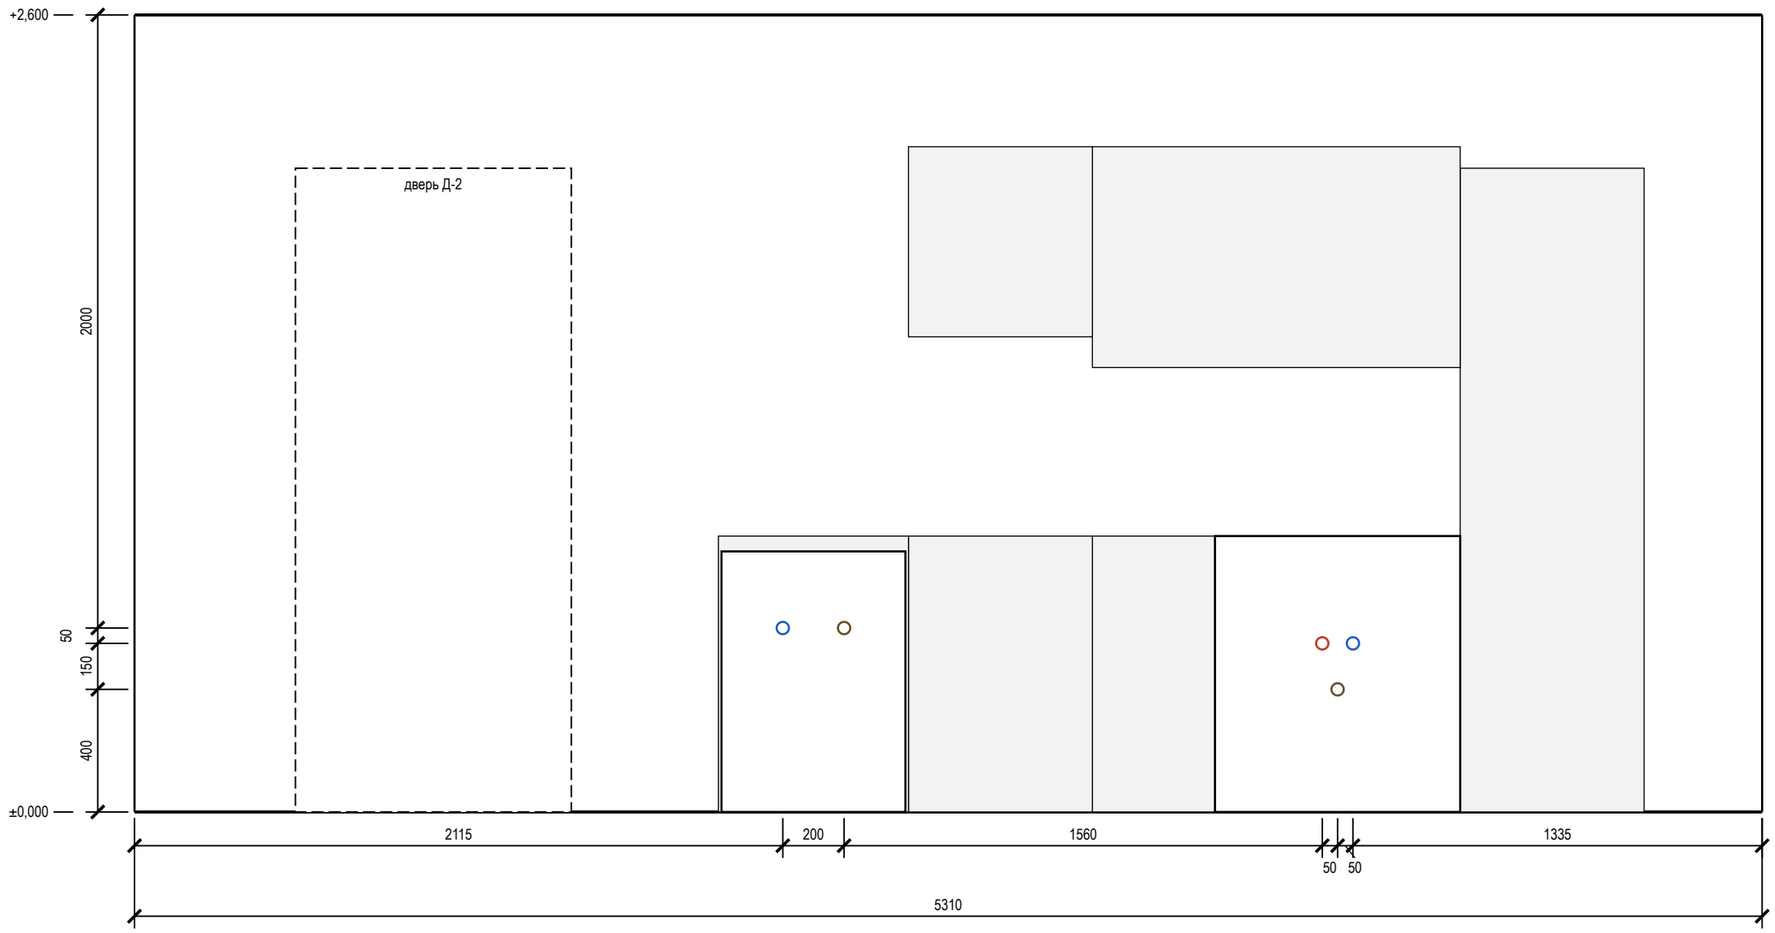


**Допущения и предложения на листе**

Основа листа: размеры сняты с плана заказчика, контрольный обмер не выполнен (К-5); высота потолка 2700 мм принята: на плане заказчика не указана (К-5); подрайон климата не задан — принят не северный (жилые от 2,5 м) (К-4); толщины стен приняты: наружные 250 мм, перегородки 120 мм — не обмерены (К-5); разрешённая мощность 15 кВт принята по типовой квартире, технических условий нет (К-6).

Знак «**» — предложение проектировщика, заказчиком не утверждено (согласовать с заказчиком): К-7: П6 — стиральная машина на кухне: в ванной и санузле места нет; подвод ХВС с шаровым краном, слив — встраиваемый сифон с обратным клапаном (водяной затвор), отдельная группа 6 щита с УЗО 30 мА.

См. лист открытых вопросов (лист 6, записи К-4–К-7).

### Ведомость привязок выводов (от чистого пола и угла)

| Код | Прибор | Ø | Н, мм | Привязка, мм |
|---|---|---|---|---|
| В1-1 | П4 мойка кухонная | ½" | 550 | ст. В: 3975 от лев. угла |
| Т3-1 | П4 мойка кухонная | ½" | 550 | ст. В: 3875 от лев. угла |
| К1-1 | П4 мойка кухонная | Ø50 | 400 | ст. В: 3925 от лев. угла |

### Ведомость привязок (продолжение)

| Код | Прибор | Ø | Н, мм | Привязка, мм |
|---|---|---|---|---|
| В1-2 | П6** стиральная машина | ½" | 600 | ст. В: 2115 от лев. угла |
| К1-2 | П6** стиральная машина | Ø40 | 600 | ст. В: 2315 от лев. угла |

### Условные обозначения

- вывод В1 (код — в ведомости привязок)
- вывод Т3 (код — в ведомости привязок)
- вывод К1 (код — в ведомости привязок)
- сантехприбор по расстановке (габарит модели)
- дверной проём; окно — сплошной контур

### Примечания

1. Габариты и высоты приборов, межосевые смесителей и места кранов — по паспортам выбранных приборов, сверяются до разметки стен.
2. Высоты Н — от чистого пола помещения, мм; отметка чистого пола и потолка — у левого края вида (от ±0,000 объекта). Привязки — от левого чистового угла вида (облицовка стен вычтена), как на развёртках стен.
3. Ревизионные люки к арматуре и ревизиям в данных не заданы: место и размер не определены (записи реестра нет).
4. Мойка, ПММ и фильтр — выводы в шкафу мойки; диаметры и положение сифона и кранов сверить по паспортам приборов и чертежам модуля.
5. Часть подписей выводов не уместилась у знака: коды и высоты — в ведомости привязок.
6. Расчёт систем водоснабжения и канализации и подбор оборудования выполняет проектная организация; лист задаёт места и высоты выводов.

1000 мм · печать 1:1

| Изм. | Кол.уч | Лист | № док. | Подп. | Дата |
|---|---|---|---|---|---|
| Разраб. | | Кырлан А.С. | | | 04.11.26 |
| Пров. | | | | | |
| ГИП | | | | | |
| | | | | | |
| Н. контр. | | | | | |
| Утв. | | | | | |

**ГД-2026-006-АИ**

Квартира 58 м²

Общая площадь 55,23* м² · * размеры приняты, не замерены (реестр — л. 6, 7, К-5)

Дизайн-проект интерьера

| Стадия | Лист | Листов |
|---|---|---|
| РП | 34 | 87 |

**Развёртки мокрых зон: выводы ВК. Кухня-гостиная**

М 1:20

**Кырлан Александр Сергеевич**


выпуск 04.11.2026 № 3da8f16a26 · стр. 39 из 96

# Развёртки мокрых зон: выводы ВК. Ванная (лист 1 из 2)


пом. 3 · выводы В1, Т3, К1 на стенах · высоты от чистого пола, привязки от чистовых углов, мм

ПРЕДВАРИТЕЛЬНО · не для производства работ · открыто пунктов: 10 (реестр — л. 6, 7)


### Стена А (М 1:20)

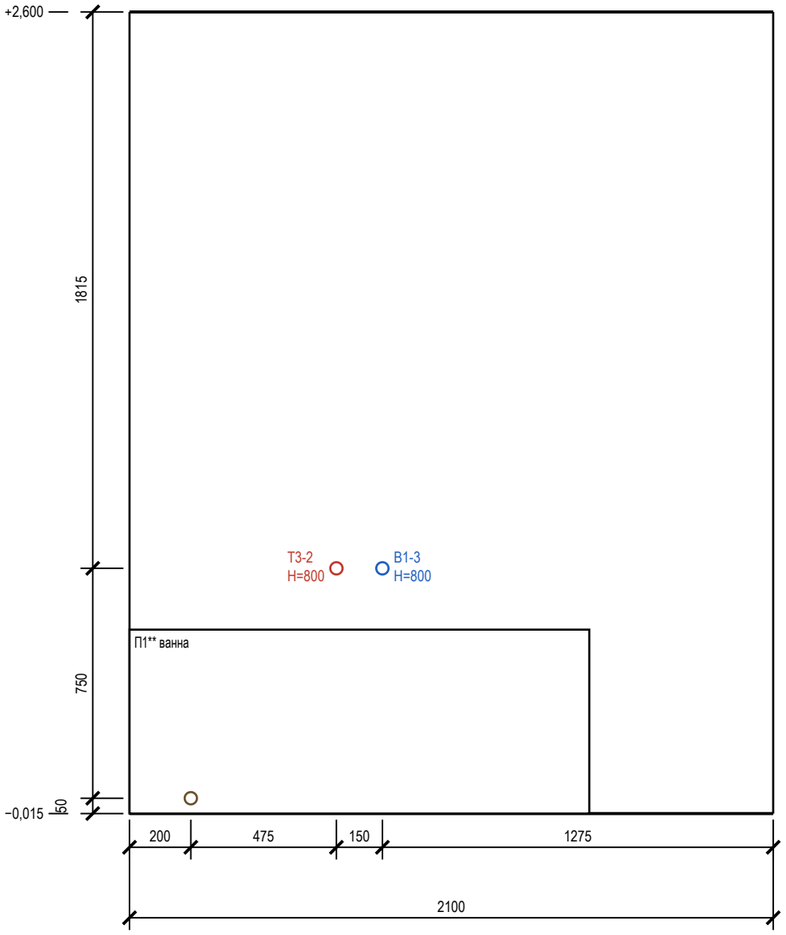


### Стена Б (М 1:20)

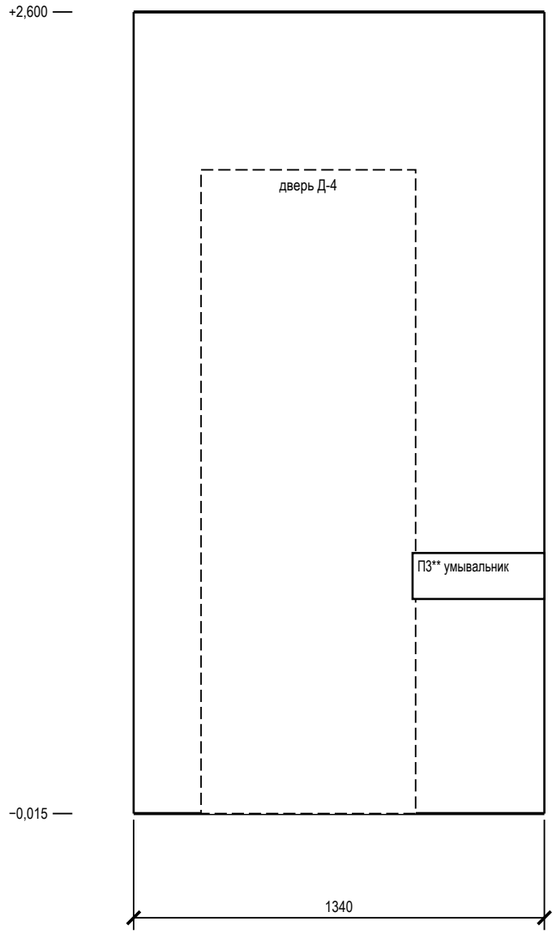


### Стена В (М 1:20)

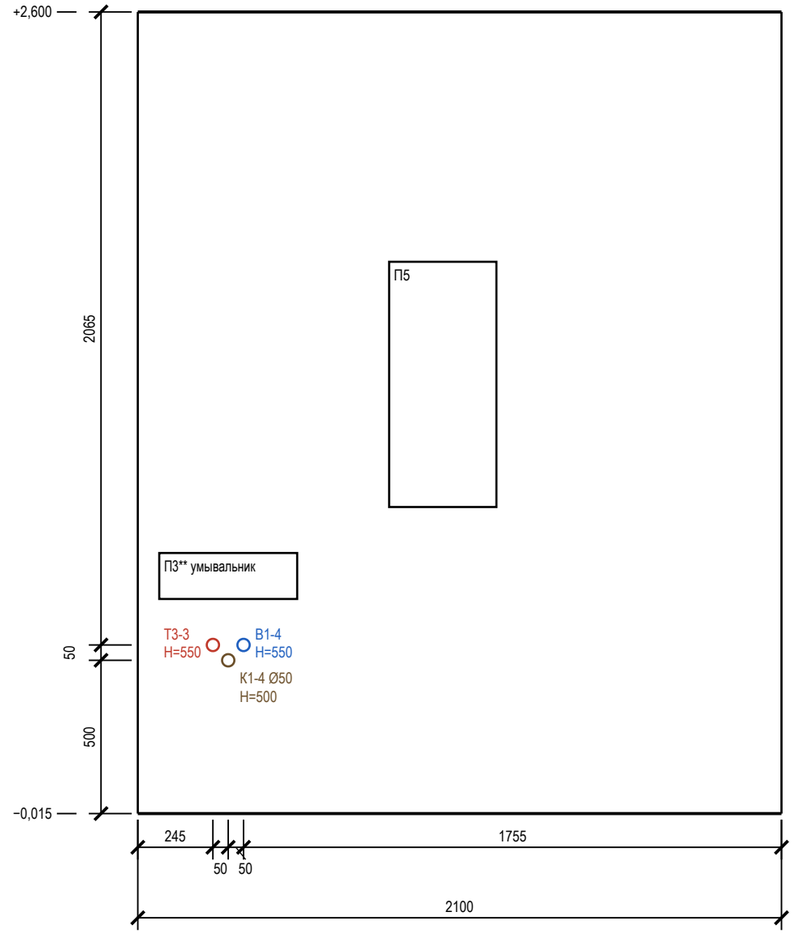


### Ведомость привязок выводов (от чистого пола и угла)

| Код | Прибор | Ø | Н, мм | Привязка, мм |
|---|---|---|---|---|
| В1-3 | П1** ванна | ½" | 800 | ст. А: 825 от лев. угла |
| Т3-2 | П1** ванна | ½" | 800 | ст. А: 675 от лев. угла |
| К1-3 | П1** ванна | Ø50 | 50 | ст. А: 200 от лев. угла |

### Ведомость привязок (продолжение)

| Код | Прибор | Ø | Н, мм | Привязка, мм |
|---|---|---|---|---|
| В1-4 | П3** умывальник | ½" | 550 | ст. В: 345 от лев. угла |
| Т3-3 | П3** умывальник | ½" | 550 | ст. В: 245 от лев. угла |
| К1-4 | П3** умывальник | Ø50 | 500 | ст. В: 295 от лев. угла |

### Условные обозначения

- вывод В1 (код — в ведомости привязок)
- вывод Т3 (код — в ведомости привязок)
- вывод К1 (код — в ведомости привязок)
- сантехприбор по расстановке (габарит модели)
- дверной проём; окно — сплошной контур

Допущения и предложения на листе. Основа листа: размеры сняты с плана заказчика, контрольный обмер не выполнен (К-5); высота потолка 2700 мм принята: на плане заказчика не указана (К-5); подрайон климата не задан — принят не северный (жилые от 2,5 м) (К-4); толщины стен приняты: наружные 250 мм, перегородки 120 мм — не обмерены (К-5); разрешённая мощность 15 кВт принята по типовой квартире, технических условий нет (К-6). Знак «**» — предложено, не утверждено (согласовать): К-2: П1, П3. См. лист открытых вопросов (лист 6, записи К-2, К-4–К-6).

### Примечания

1. Габариты и высоты приборов, межосевые смесителей и места кранов — по паспортам выбранных приборов, сверяются до разметки стен.
2. Высоты Н — от чистого пола помещения, мм; отметка чистого пола и потолка — у левого края вида (от ±0,000 объекта). Привязки — от левого чистового угла вида (облицовка стен вычтена), как на развёртках стен.
3. Стояки в помещении: Ст К1-1 Ø110, Ст В1-1 Ø32, Ст Т3-1 Ø32 — положение на плане выводов; выводы подключаются к ним по схеме разводки.
4. Ревизионные люки к арматуре и ревизиям в данных не заданы: место и размер не определены (записи реестра нет).
5. Часть подписей выводов не уместилась у знака: коды и высоты — в ведомости привязок.
6. Помещение «Ванная» — 2 листа: стены 1) А, Б, В; 2) Г.
7. Расчёт систем водоснабжения и канализации и подбор оборудования выполняет проектная организация; лист задаёт места и высоты выводов.

1000 мм · печать 1:1

| Изм. | Кол.уч | Лист | № док. | Подп. | Дата |
|---|---|---|---|---|---|
| Разраб. | | Кырлан А.С. | | | 04.11.26 |
| Пров. | | | | | |
| ГИП | | | | | |
| | | | | | |
| Н. контр. | | | | | |
| Утв. | | | | | |

**ГД-2026-006-АИ**

Квартира 58 м²

Общая площадь 55,23* м² · * размеры приняты, не замерены (реестр — л. 6, 7, К-5)

Дизайн-проект интерьера

| Стадия | Лист | Листов |
|---|---|---|
| РП | 35 | 87 |

**Развёртки мокрых зон: выводы ВК. Ванная (лист 1 из 2)**

М 1:20

**Кырлан Александр Сергеевич**


выпуск 04.11.2026 № 3da8f16a26 · стр. 40 из 96

# Развёртки мокрых зон: выводы ВК. Ванная (лист 2 из 2)

ПРЕДВАРИТЕЛЬНО · не для производства работ · открыто пунктов: 10 (реестр — л. 6, 7)

пом. 3 · выводы В1, Т3, К1 на стенах · высоты от чистого пола, привязки от чистовых углов, мм

### Стена Г (М 1:20)

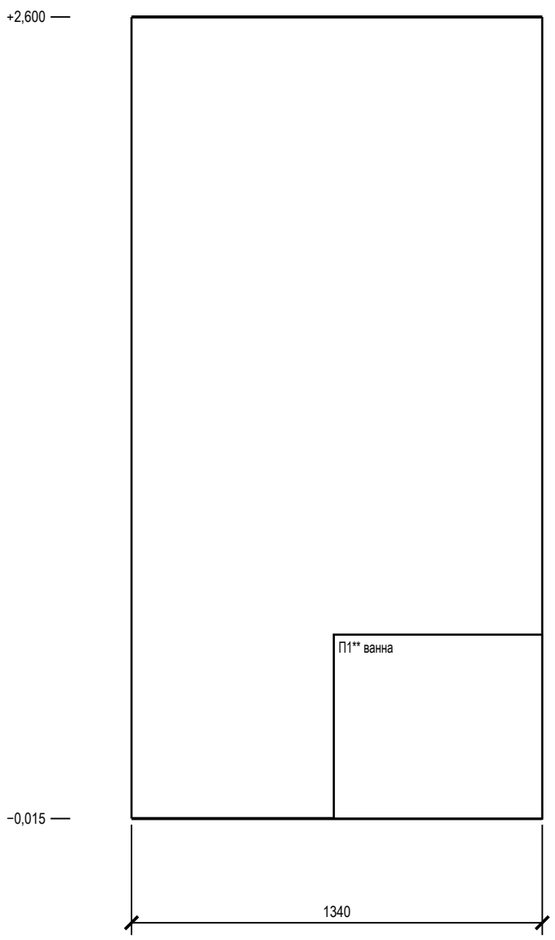


### Ведомость привязок выводов (от чистого пола и угла)

| Код | Прибор | Ø | H, мм | Привязка, мм |
|---|---|---|---|---|
| | выводов на стене нет | | | |

**Допущения и предложения на листе**

Основа листа: размеры сняты с плана заказчика, контрольный обмер не выполнен (К-5); высота потолка 2700 мм принята: на плане заказчика не указана (К-5); подрайон климата не задан — принят не северный (жилые от 2,5 м) (К-4); толщины стен приняты: наружные 250 мм, перегородки 120 мм — не обмерены (К-5); разрешённая мощность 15 кВт принята по типовой квартире, технических условий нет (К-6).

Знак «**» — предложение проектировщика, заказчиком не утверждено (согласовать с заказчиком): К-2: П1 — ванна 1500 вместо 1600 — не заходит в проход перед проёмом Д-4; перед ванной 680 мм — глубина помещения.

См. лист открытых вопросов (лист 6, записи К-2, К-4–К-6).

### Условные обозначения

- вывод В1 (код — в ведомости привязок)
- вывод Т3 (код — в ведомости привязок)
- вывод К1 (код — в ведомости привязок)
- сантехприбор по расстановке (габарит модели)
- дверной проём; окно — сплошной контур

### Примечания

1. Габариты и высоты приборов, межосевые смесителей и места кранов — по паспортам выбранных приборов, сверяются до разметки стен.
2. Высоты Н — от чистого пола помещения, мм; отметка чистого пола и потолка — у левого края вида (от ±0,000 объекта). Привязки — от левого чистового угла вида (облицовка стен вычтена), как на развёртках стен.
3. Стояки в помещении: Ст К1-1 Ø110, Ст В1-1 Ø32, Ст Т3-1 Ø32 — положение на плане выводов; выводы подключаются к ним по схеме разводки.
4. Ревизионные люки к арматуре и ревизиям в данных не заданы: место и размер не определены (записи реестра нет).
5. Помещение «Ванная» — 2 листа: стены 1) А, Б, В; 2) Г.
6. Расчёт систем водоснабжения и канализации и подбор оборудования выполняет проектная организация; лист задаёт места и высоты выводов.

1000 мм · печать 1:1

| Изм. | Кол.уч | Лист | № док. | Подп. | Дата |
|---|---|---|---|---|---|
| Разраб. | | Кырлан А.С. | | | 04.11.26 |
| Пров. | | | | | |
| ГИП | | | | | |
| | | | | | |
| Н. контр. | | | | | |
| Утв. | | | | | |

**ГД-2026-006-АИ**

Квартира 58 м²

Общая площадь 55,23* м² · * размеры приняты, не замерены (реестр — л. 6, 7, К-5)

Дизайн-проект интерьера

| Стадия | Лист | Листов |
|---|---|---|
| РП | 36 | 87 |

**Развёртки мокрых зон: выводы ВК. Ванная (лист 2 из 2)**

М 1:20

**Кырлан Александр Сергеевич**


выпуск 04.11.2026 № 3da8f16a26 · стр. 41 из 96

# Развёртки мокрых зон: выводы ВК. Санузел

пом. 4 · выводы B1, T3, K1 на стенах · высоты от чистого пола, привязки от чистовых углов, мм

ПРЕДВАРИТЕЛЬНО · не для производства работ · открыто пунктов: 10 (реестр — л. 6, 7)

### Стена Г (М 1:20)

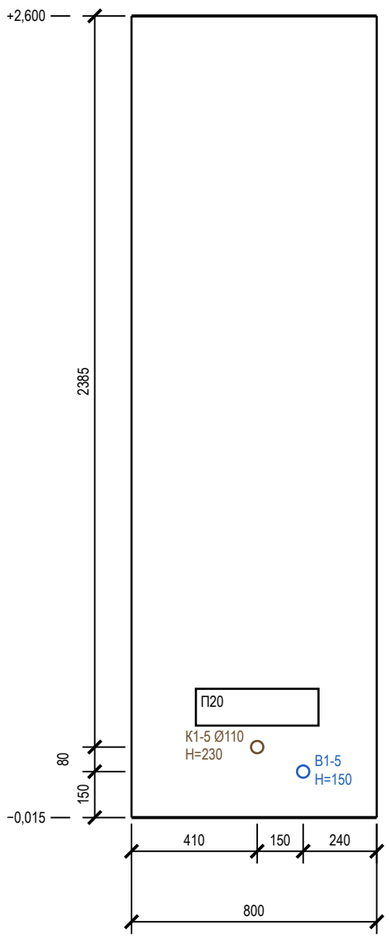


### Ведомость привязок выводов (от чистого пола и угла)

| Код | Прибор | Ø | H, мм | Привязка, мм |
|---|---|---|---|---|
| B1-5 | П20 унитаз подвесной | ½" | 150 | ст. Г: 560 от лев. угла |
| K1-5 | П20 унитаз подвесной | Ø110 | 230 | ст. Г: 410 от лев. угла |

### Условные обозначения

- вывод B1 (код — в ведомости привязок)
- вывод T3 (код — в ведомости привязок)
- вывод K1 (код — в ведомости привязок)
- сантехприбор по расстановке (габарит модели)
- дверной проём; окно — сплошной контур

### Примечания

1. Габариты и высоты приборов, межосевые смесителей и места кранов — по паспортам выбранных приборов, сверяются до разметки стен.
2. Высоты H — от чистого пола помещения, мм; отметка чистого пола и потолка — у левого края вида (от ±0,000 объекта). Привязки — от левого чистового угла вида (облицовка стен вычтена), как на развёртках стен.
3. Ревизионные люки к арматуре и ревизиям в данных не заданы: место и размер не определены (записи реестра нет).
4. Расчёт систем водоснабжения и канализации и подбор оборудования выполняет проектная организация; лист задаёт места и высоты выводов.

**Допущения и предложения на листе**

Основа листа: размеры сняты с плана заказчика, контрольный обмер не выполнен (К-5); высота потолка 2700 мм принята: на плане заказчика не указана (К-5); подрайон климата не задан — принят не северный (жилые от 2,5 м) (К-4); толщины стен приняты: наружные 250 мм, перегородки 120 мм — не обмерены (К-5); разрешённая мощность 15 кВт принята по типовой квартире, технических условий нет (К-6).

См. лист открытых вопросов (лист 6, записи К-4–К-6).

1000 мм · печать 1:1

| Изм. | Кол.уч | Лист | № док. | Подп. | Дата |
|---|---|---|---|---|---|
| Разраб. | | Кырлан А.С. | | | 04.11.26 |
| Пров. | | | | | |
| ГИП | | | | | |
| | | | | | |
| Н. контр. | | | | | |
| Утв. | | | | | |

**ГД-2026-006-АИ**

Квартира 58 м²

Общая площадь 55,23* м² · * размеры приняты, не замерены (реестр — л. 6, 7, К-5)

Дизайн-проект интерьера

| Стадия | Лист | Листов |
|---|---|---|
| РП | 37 | 87 |

**Развёртки мокрых зон: выводы ВК. Санузел**

М 1:20

**Кырлан Александр Сергеевич**

выпуск 04.11.2026 № 3da8f16a26 · стр. 42 из 96

# Спецификация сантехнического оборудования

Форма 1 ГОСТ 21.110-2013 · ГД-2026-006-АИ-ВК.СО · приборы, арматура, трубопроводы

**ПРЕДВАРИТЕЛЬНО · не для производства работ · открыто пунктов: 10 (реестр — л. 6, 7)**

| Поз. | Наименование и техническая характеристика | Тип, марка, обозначение документа | Код продукции | Поставщик | Ед. изм. | Кол. | Масса 1 ед., кг | Примечание |
|---|---|---|---|---|---|---|---|---|
| | Санитарные приборы | | | | | | | |
| 1 | Ванна встраиваемая акриловая 1500×700 мм, с каркасом, экраном и отверстием слив-перелив | акриловая 1500×700, смеситель настенный | | выбор заказчика | шт | 1 | | П1** |
| 2 | Унитаз подвесной безободковый, с сиденьем микролифт, крепёж и звукоизолирующая прокладка | Laufen Pro 8.2096.6.000.000.1 | | выбор заказчика | шт | 1 | | П20 |
| 3 | Инсталляция для подвесного унитаза: рама высотой 1120 мм, бачок, клавиша смыва (ось клавиши 1050 мм от чистого пола) | аналог | | выбор заказчика | шт | 1 | | П20; короб ГКЛВ |
| 4 | Умывальник подвесной 450×450 мм, с отверстием под смеситель и переливом | Laufen Pro S 8.1096.3.000.104.1 | | выбор заказчика | шт | 1 | | П3** |
| 5 | Мойка кухонная 700×480 мм, с переливом | мойка врезная 700×480 в шкафу М5 | | с кухонной мебелью | шт | 1 | | П4 |
| 6 | Полотенцесушитель электрический, IP44, с терморегулятором | аналог | | выбор заказчика | шт | 1 | | П5 |
| | Смесители, сифоны и арматура приборов | | | | | | | |
| 7 | Смеситель для ванны настенный однорычажный, межосевое 150 мм, с душевым набором (лейка, шланг, держатель) | аналог | | выбор заказчика | шт | 1 | | П1** |
| 8 | Смеситель для умывальника однорычажный, с донным клапаном | аналог | | выбор заказчика | шт | 1 | | П3** |
| 9 | Смеситель кухонный однорычажный, высокий излив | аналог | | выбор заказчика | шт | 1 | | П4 |
| 10 | Обвязка ванны слив-перелив Ø40/50 с сифоном | аналог | | выбор заказчика | шт | 1 | | П1** |
| 11 | Сифон для умывальника бутылочный Ø32/40–50, с гофрой к выпуску | аналог | | выбор заказчика | шт | 1 | | П3** |
| 12 | Сифон для мойки Ø40/50 | аналог | | выбор заказчика | шт | 1 | | П4 |
| 13 | Сифон для стиральной машины встраиваемый в стену Ø50, с обратным клапаном | аналог | | выбор заказчика | шт | 1 | | П6** |
| 14 | Кран угловой ½"×½" с гибкой подводкой 40 см (умывальники, мойка) | аналог | | выбор заказчика | шт | 4 | | по 2 на прибор |
| 15 | Кран шаровой угловой ½"×¾" для подключения стиральной и посудомоечной машины | аналог | | выбор заказчика | шт | 1 | | П6** |
| | Трубопроводы | | | | | | | |
| 16 | Труба полипропиленовая PP-R PN20 Ø20×3,4 (В1) | ГОСТ 32415-2013 | | выбор заказчика | м | 13,5 | 0,17 | 9,2 + 2,6 + 10 % |
| 17 | Труба PP-R, армированная стекловолокном, PN20 Ø20×2,8 (Т3) | ГОСТ 32415-2013 | | выбор заказчика | м | 9,5 | 0,15 | 6,4 + 1,9 + 10 % |
| 18 | Труба канализационная ПП Ø40 (К1) | ГОСТ 32414-2013 | | выбор заказчика | м | 2,5 | | 1,7 + 0,6 + 10 % |
| 19 | Труба канализационная ПП Ø50 (К1) | ГОСТ 32414-2013 | | выбор заказчика | м | 8 | | 6,1 + 0,9 + 10 % |
| 20 | Труба канализационная ПП Ø110 (К1) | ГОСТ 32414-2013 | | выбор заказчика | м | 1,5 | | 0,8 + 0,2 + 10 % |
| | Фасонные части и выводы | | | | | | | |
| 21 | Отвод канализационный ПП 45° Ø40 | ГОСТ 32414-2013 | | выбор заказчика | шт | 2 | | 2 шт. на поворот |
| 22 | Отвод канализационный ПП 45° Ø50 | ГОСТ 32414-2013 | | выбор заказчика | шт | 12 | | 2 шт. на поворот |
| 23 | Отвод канализационный ПП 45° Ø110 | ГОСТ 32414-2013 | | выбор заказчика | шт | 6 | | 2 шт. на поворот |
| 24 | Тройник канализационный ПП 45° (врезки ветвей) | ГОСТ 32414-2013 | | выбор заказчика | шт | 4 | | |
| 25 | Ревизия канализационная ПП (после поворота трассы) | ГОСТ 32414-2013 | | выбор заказчика | шт | 5 | | доступ сохранить |
| 26 | Фитинги PP-R Ø20: тройники, угольники 90° (ветви и повороты В1, Т3) | ГОСТ 32415-2013 | | выбор заказчика | шт | 22 | | |
| 27 | Водорозетка PP-R Ø20×½" настенная, с креплением | ГОСТ 32415-2013 | | выбор заказчика | шт | 8 | | коды — лист выводов |
| | Узлы ввода, люки, короба | | | | | | | |
| 28 | Кран шаровой латунный Ду15 PN16 (отключение ввода) | аналог | | выбор заказчика | шт | 2 | | Ст В1-1, Ст Т3-1 |
| 29 | Фильтр сетчатый косой Ду15 | аналог | | выбор заказчика | шт | 2 | | |
| 30 | Счётчик воды крыльчатый Ду15 (ХВ, ГВ), с поверкой | аналог | | выбор заказчика | шт | 2 | | пломба УК |
| 31 | Клапан обратный Ду15 | аналог | | выбор заказчика | шт | 2 | | |
| 32 | Люк ревизионный нажимной под плитку 300×400 мм | аналог | | выбор заказчика | шт | 1 | | к стоякам и арматуре |
| 33 | Звукоизоляция стояка К1 в коробе: рулонный звукоизоляционный материал ≥ 10 мм, обмотка стояка на высоту этажа | аналог | | выбор заказчика | м | 2,7 | | Ст К1-1 |
| 34 | Короб К1 над полом: профиль ПН/ПС, ГКЛВ 12,5 мм под плитку | аналог | | выбор заказчика | м | 1,6 | | сечение — лист разводки |

## Примечания

1. Форма 1 ГОСТ 21.110-2013, ширины граф изменены по п. 4.1. «Аналог» — аналог по характеристикам: модели внести до черновых работ, привязки выводов сверить по паспортам.
2. Бытовая техника не входит (показана арматура подключения), мойка — в комплекте кухни (марка — модуля кухни, как у столяра). Длины труб — трасса листа разводки + подъёмы + 10 %.
3. Стояк К1 в коробе — звукоизоляция стояка в коробе без жёсткого контакта короба с трубой.
4. Расчёт систем водоснабжения и канализации, диаметры магистралей и подбор оборудования выполняет проектная организация.

**Допущения и предложения на листе**

Основа листа: размеры сняты с плана заказчика, контрольный обмер не выполнен (К-5); высота потолка 2700 мм принята: на плане заказчика не указана (К-5); подрайон климата не задан — принят не северный (жилые от 2,5 м) (К-4); толщины стен приняты: наружные 250 мм, перегородки 120 мм — не обмерены (К-5); разрешённая мощность 15 кВт принята по типовой квартире, технических условий нет (К-6).

Знак «**» — предложение проектировщика, заказчиком не утверждено (согласовать с заказчиком): К-2: П1 — ванна 1500 вместо 1600 — не заходит в проход перед проёмом Д-4; перед ванной 680 мм — глубина помещения; П3 — умывальник у стены В справа от ванны — перед ним свободно 750 мм, до стены Б 90 мм; К-7: П6 — стиральная машина на кухне: в ванной и санузле места нет; подвод ХВС с шаровым краном, слив — встраиваемый сифон с обратным клапаном (водяной затвор), отдельная группа 6 щита с УЗО 30 мА.

См. лист открытых вопросов (лист 6, записи К-2, К-4–К-7).

| Изм. | Кол.уч | Лист | № док. | Подп. | Дата | ГД-2026-006-АИ | | | |
|---|---|---|---|---|---|---|---|---|---|
| | | | | | | Квартира 58 м² | | | |
| | | | | | | Общая площадь 55,23* м² · * размеры приняты, не замерены (реестр — л. 6, 7, К-5) | | | |
| Разраб. | | Кырлан А.С. | | | 04.11.26 | Дизайн-проект интерьера | Стадия | Лист | Листов |
| Пров. | | | | | | | РП | 38 | 87 |
| ГИП | | | | | | | | | |
| Н. контр. | | | | | | Спецификация сантехнического оборудования | Кырлан Александр Сергеевич | | |
| Утв. | | | | | | М б/м | | | |

выпуск 04.11.2026 № 3da8f16a26 · стр. 43 из 96

# Техническое задание на подбор светильников

ПРЕДВАРИТЕЛЬНО · не для производства работ · открыто пунктов: 10 (реестр — л. 6, 7)

Параметры для подбора: светильники, ленты и блоки питания, слои света · б/м

## Параметры светильников для подбора

| Поз. | Марки | Наименование | Установка | Кол. | P, Вт | Σ P, Вт | Ф, лм | Тц, К | Ra | Угол, ° | IP | Дим. | Слой | Группа | Пом. |
|---|---|---|---|---|---|---|---|---|---|---|---|---|---|---|---|
| 1 | Св1** | Подвесной | подвес, низ H=1450 | 1 | 40 | 40 | 3600 | 3000 | 90 | — | 20 | — | общий | L1 | 1 |
| 2 | Св2** | Трековая система | на потолке | 4 | 12 | 48 | 950 | 3000 | 90 | — | 20 | — | общий | L5 | 1 |
| 3 | Св3 | Линейный настенный | под верхними шкафами, H=1400 | 1 | 14 | 14 | 1080 | 3000 | 90 | — | 20 | — | рабочий | L6 | 1 |
| 4 | Св4 | Потолочный накладной | на потолке | 1 | 36 | 36 | 3200 | 2700 | 90 | — | 20 | — | общий | L2 | 2 |
| 5 | Св5** | Трековая система | на потолке | 2 | 12 | 24 | 900 | 2700 | 90 | — | 20 | — | общий | L2 | 2 |
| 6 | Св6, Св7 | Настенный (бра) | на стене, H=1300 | 2 | 4 | 8 | 250 | 2700 | 90 | — | 20 | — | рабочий | L8 | 2 |
| 7 | Св8 | Встраиваемый точечный | в ГКЛ, корпус ≤ 70 мм | 1 | 9 | 9 | 700 | 3000 | 90 | — | 44 | — | общий | L4 | 3 |
| 8 | Св9** | Настенный (бра) | над зеркалом, H=1900 | 1 | 6 | 6 | 400 | 3000 | 90 | — | 44 | — | рабочий | L4 | 3 |
| 9 | Св10 | Встраиваемый точечный | в ГКЛ, корпус ≤ 70 мм | 1 | 6 | 6 | 500 | 3000 | 90 | — | 44 | — | общий | L9 | 4 |
| 10 | Св11, Св12 | Встраиваемый точечный | в ГКЛ, корпус ≤ 70 мм | 2 | 9 | 18 | 800 | 3000 | 90 | — | 20 | — | общий | L3 | 5 |
| 11 | Св16 | Потолочный накладной | на потолке, засветка стены | 1 | 10 | 10 | 900 | 3000 | 90 | — | 20 | — | общий | L7 | 6 |
| | | **Итого** | | **17 шт** | | **219** | | | | | | | | | |

## Слои света по помещениям

| Пом. | Помещение | Слои света — группы включения (марки — в спецификации) | Σ P, Вт |
|---|---|---|---|
| 1 | Кухня-гостиная | общий — L1, L5; рабочий — L6 | 102 |
| 2 | Спальня | общий — L2; рабочий — L8 | 68 |
| 3 | Ванная | общий — L4; рабочий — L4 | 15 |
| 4 | Санузел | общий — L9 | 6 |
| 5 | Прихожая | общий — L3 | 18 |
| 6 | Гардеробная | общий — L7 | 10 |

## LED-ленты, линейные светильники и блоки питания

| Марка | Пом. | L, м | U, В | Вт/м | Σ P, Вт | БП | P БП, Вт | Загр., % | Питание | Доступ к БП |
|---|---|---|---|---|---|---|---|---|---|---|
| Св2** | 1 | 1,2 | 24 | — | 48 | БП1 | 100 | 62 | встроенный ввод | H=2300 |
| — | 1 | 1,8 | 24 | — | 14 | БП1 | 100 | 62 | встроенный ввод | H=2300 |
| Св5** | 2 | 0,8 | 24 | — | 24 | БП2 | 60 | 40 | встроенный ввод | H=2300 |

## Слои света

общий — равномерный свет помещения, по норме освещённости

рабочий — местный свет задачи: столешница, зеркало, чтение у кровати

**Допущения и предложения на листе**

Основа листа: размеры сняты с плана заказчика, контрольный обмер не выполнен (К-5); высота потолка 2700 мм принята: на плане заказчика не указана (К-5); подрайон климата не задан — принят не северный (жилые от 2,5 м) (К-4); толщины стен приняты: наружные 250 мм, перегородки 120 мм — не обмерены (К-5); разрешённая мощность 15 кВт принята по типовой квартире, технических условий нет (К-6).

Знак «**» — предложение проектировщика, заказчиком не утверждено (согласовать с заказчиком): Св2 — общий свет зоны гостиной над журнальным столом М21 (трек шёл вдоль края стола М3 по проходу); трековая система 4 × 950 лм: поток принят до нормы освещённости, модель и паспорт не выбраны; Св5 — трековая система 2 × 900 лм: светильник добавлен проектировщиком, поток принят до нормы освещённости, модель и паспорт не выбраны; Св1 — подвес висел над проходом без заданной высоты, а стол — без света над ним: подвес по оси стола М3; Св9 — свет у зеркала — над зеркалом у умывальника по его оси (свет на лицо, а не над сантехникой).

См. лист открытых вопросов (лист 6, записи К-4–К-6).

## Примечания

1. Позиции и марки Св — те же, что на плане освещения (лист 21) и в ведомости светильников (лист 23); группы L — по плану выключателей (лист 22).
2. Модели светильников не выбраны: лист — техническое задание на подбор. Модель по строке таблицы: поток, Тц, Ra, угол, IP и регулировка яркости не хуже указанных, мощность не больше; встраиваемые — под глубину короба (графа «Установка»). IP 20 — сухие помещения. После выбора моделей (артикул, производитель) лист выпускается как «Спецификация светильников».
3. Мощность и поток в таблице — требования к подбору (поток не меньше, мощность не больше указанных); после выбора модели — по её паспорту, Σ P — установленная мощность освещения. Оценка освещённости — на плане освещения; это не светотехнический расчёт.

| Изм. | Кол.уч | Лист | № док. | Подп. | Дата |
|---|---|---|---|---|---|
| Разраб. | | Кырлан А.С. | | | 04.11.26 |
| Пров. | | | | | |
| ГИП | | | | | |
| | | | | | |
| Н. контр. | | | | | |
| Утв. | | | | | |

**ГД-2026-006-АИ**

Квартира 58 м²

Общая площадь 55,23* м² · * размеры приняты, не замерены (реестр — л. 6, 7, К-5)

Дизайн-проект интерьера

| Стадия | Лист | Листов |
|---|---|---|
| РП | 39 | 87 |

**Техническое задание на подбор светильников**

М б/м

**Кырлан Александр Сергеевич**

выпуск 04.11.2026 № 3da8f16a26 · стр. 44 из 96

06

# Потолки и ГКЛ-конструкции

Кырлан Александр Сергеевич


выпуск 04.11.2026 · 3da8f16a26 · стр. 45 из 96

# План потолков

Уровни и марки потолков, короба с подсветкой, ниши под шторы, люки, вырезы · отметки низа от ±0,000 чистого пола · размеры в мм

**ПРЕДВАРИТЕЛЬНО · не для производства работ · открыто пунктов: 10 (реестр — л. 6, 7)**

Допущения и предложения на листе. Основа листа: размеры сняты с плана заказчика, контрольный обмер не выполнен (К-5); высота потолка 2700 мм принята: на плане заказчика не указана (К-5); подрайон климата не задан — принят не северный (жилые от 2,5 м) (К-4); толщины стен приняты: наружные 250 мм, перегородки 120 мм — не обмерены (К-5); разрешённая мощность 15 кВт принята по типовой квартире, технических условий нет (К-6). См. лист открытых вопросов (лист 6, записи К-4–К-6); по листу — К-4.

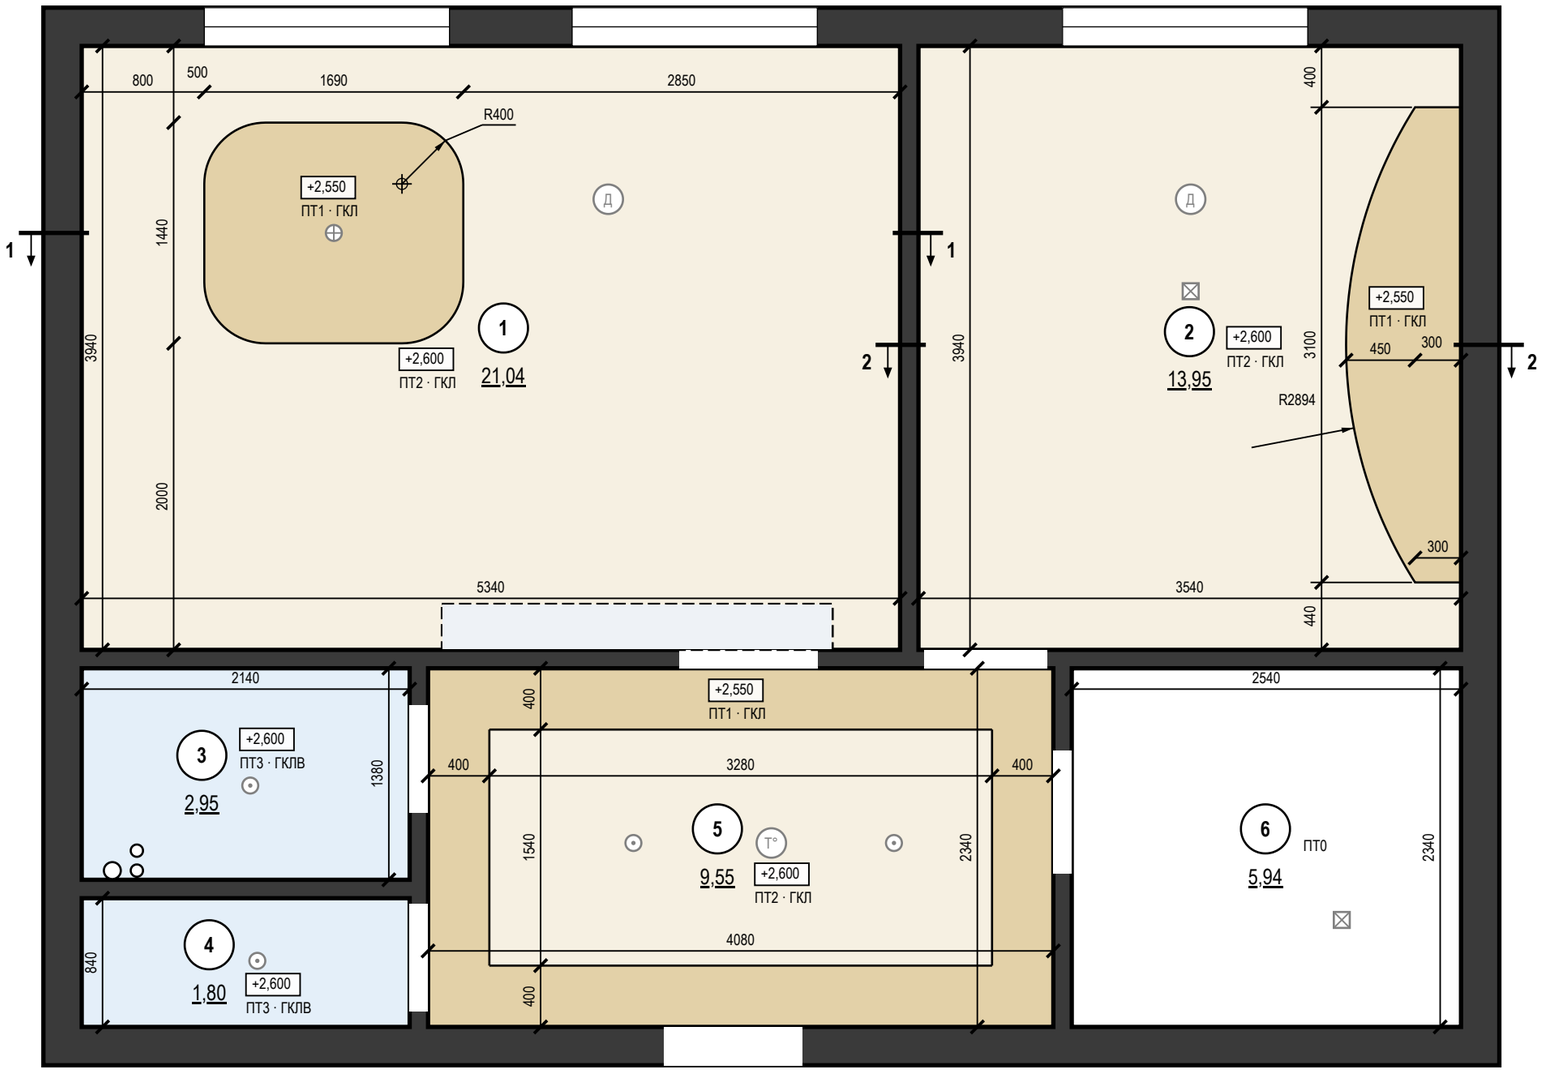


## Ведомость потолков

| Пом. | Марка | Конструкция | Низ / верх ниши | S, м² | Q |
|---|---|---|---|---|---|
| 1 | ПТ1 | ГКЛ П113, остров | +2,550 | 2,30 | Q3 |
| 1 | ПТ2 | ГКЛ П113 | +2,600 | 18,74 | Q3 |
| 2 | ПТ1 | ГКЛ П113, дуга | +2,550 | 1,88 | Q3 |
| 2 | ПТ2 | ГКЛ П113 | +2,600 | 12,07 | Q3 |
| 3 | ПТ3 | ГКЛВ П113 | +2,600 | 2,95 | Q3 |
| 4 | ПТ3 | То же | +2,600 | 1,80 | Q3 |
| 5 | ПТ1 | ГКЛ П113 | +2,550 | 4,50 | Q3 |
| 5 | ПТ2 | ГКЛ П113 | +2,600 | 5,05 | Q3 |
| 6 | ПТ0 | Существующий потолок, окраска | +2,700 | 5,94 | |
| | | **Итого** | | **55,23** | |

## Ведомость вырезов и закладных в потолке

| Марка | Устройство | Кол. | Пом. |
|---|---|---|---|
| | Светильник встраиваемый (марки — план освещения) | 4 | 3, 4, 5 |
| | Светильник накладной (марки — план освещения) | 2 | 2, 6 |
| | Светильник подвесной (марки — план освещения) | 1 | 1 |
| | Извещатель дымовой | 2 | 1, 2 |
| | Извещатель тепловой | 1 | 5 |

## Условные обозначения

- ПТ1 — ГКЛ по каркасу П113, низ +2,550
- ПТ2 — ГКЛ по каркасу П113, низ +2,600
- ПТ3 — ГКЛВ по каркасу П113, низ +2,600
- ПТ0 — существующий потолок, окраска, без подвесного потолка, низ +2,700
- граница уровней потолка (перепад)
- стояк: К1 — канализация, В1 — ХВС, Т3 — ГВС
- светильник подвесной — подложка с плана освещения
- светильник накладной — подложка с плана освещения
- светильник встраиваемый — подложка с плана освещения
- Д — извещатель дымовой на потолке — подложка
- T° — извещатель тепловой на потолке — подложка
- короб воздуховода вытяжки ГКЛ (трасса — план вентиляции)
- линия разреза у стен помещения, стрелка — направление взгляда
- +2,600 — отметка низа потолка, м (у ниши под шторы — верх ниши); под ней марка потолка
- 1 — номер помещения, площадь м²

## Примечания

1. За отметку ±0,000 принят уровень чистого пола сухих помещений (готовое покрытие), а не существующего пола; пол пом. 3, 4 — −0,015; верх плиты перекрытия −0,064 — расчётный по пирогу пола, не замерен; существующий пол снимается до плиты, его отметка не замерена. Отметки в прямоугольниках — низ потолка; низ перекрытия +2,700. Марка потолка — одна конструкция и отметка на весь альбом.
2. Размеры помещений в свету (ширина × длина, мм), не поместившиеся на плане: пом. 4 — 2140 × 840.
3. Потолки ГКЛ — каркасная система П113: подвесы через 1000 (с запасом: СП 163, табл. 14 — до 1100 при 0,15 кН/м²), несущие профили через 500, основные через 1200 мм; листы — поперёк несущих профилей. В помещениях 3, 4 — ГКЛВ на оцинкованном каркасе.
4. Нижний уровень — пояс-короб по периметру шириной 400 мм, верхний — поле внутри пояса: пом. 5.
5. Примыкание к стенам: теневой шов 15 мм, техзазор 3 мм — пом. 1, 2, 5, по стенам, выровненным штукатуркой (узел 1); пом. 3, 4 — разделительная лента.
6. Светильники и потолочные устройства — подложка с планов освещения, слаботочных систем и вентиляции (положение — по ним); вырезы и закладные — по ведомости на листе, до обшивки; отверстия не совмещать с профилями, глубина корпуса светильника до 70 мм.
7. Разрезы 1–1, 2–2 — на листе 41; высоты мебели и дверных блоков сверены с низом потолка в разрезах; гибка бортов фигур и ленты ниш — там же; размеры фигурных уровней — фрагменты 1, 2 (лист 42).
8. Шпаклевание ГКЛ и условия приёмки — Q3: рассеянный дневной свет, осмотр с 2 м; боковой свет не оценивается.
9. Пом. 1: короб воздуховода кухонной вытяжки ГКЛ 300×200 мм (ширина от стены × высота), низ +2,500, длина 2,25 м — по трассе плана вентиляции, вдоль стен до входа в канал под воздуховод Ø125; каркас ПН 28×27 по стене и плите, ПП 60×27, лист ГКЛ 12,5.

1000 мм · печать 1:1

| Изм. | Кол.уч | Лист | № док. | Подп. | Дата |
|---|---|---|---|---|---|
| Разраб. | | Кырлан А.С. | | | 04.11.26 |
| Пров. | | | | | |
| ГИП | | | | | |
| | | | | | |
| Н. контр. | | | | | |
| Утв. | | | | | |

**ГД-2026-006-АИ**

Квартира 58 м²

Общая площадь 55,23* м² · * размеры приняты, не замерены (реестр — л. 6, 7, К-5)

Дизайн-проект интерьера

| Стадия | Лист | Листов |
|---|---|---|
| РП | 40 | 87 |

**План потолков**

М 1:40

**Кырлан Александр Сергеевич**


выпуск 04.11.2026 № 3da8f16a26 · стр. 46 из 96

# Разрезы и узлы потолков

Разрезы по потолкам с отметками уровней · размеры в мм


### Разрез 1–1 (М 1:40)

Пом. 1 Кухня-гостиная; линия разреза — план потолков, лист 40

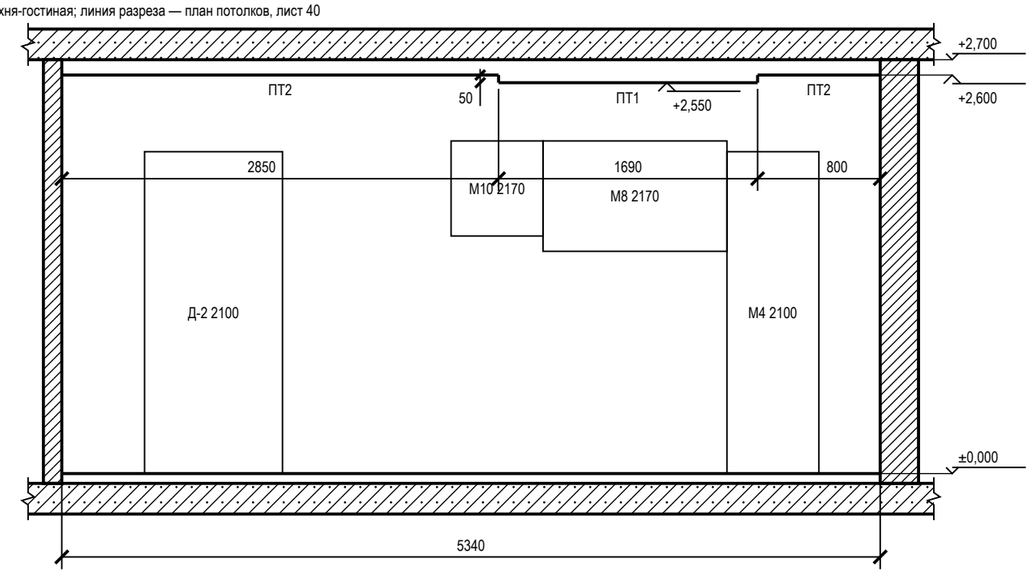


### Разрез 2–2 (М 1:40)

Пом. 2 Спальня; линия разреза — план потолков, лист 40

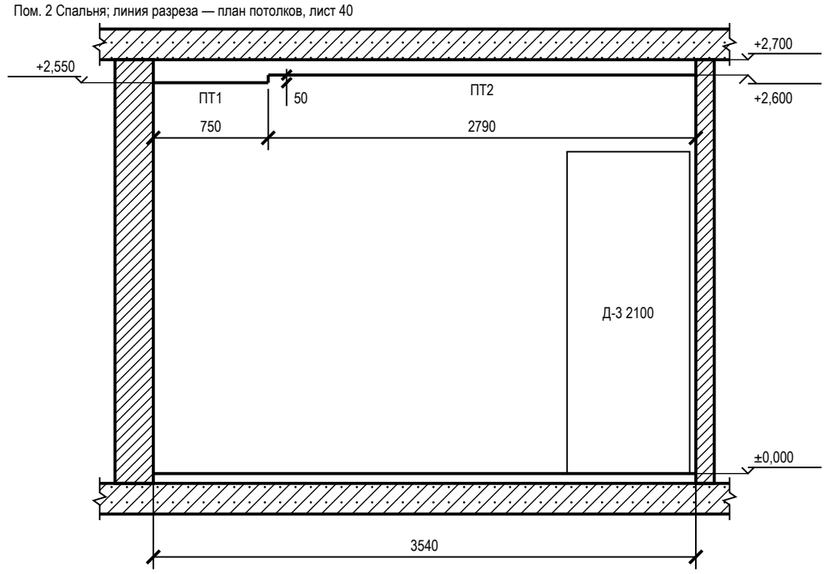


### Условные обозначения

- плита перекрытия в сечении
- стена в сечении
- потолок ГКЛ в сечении; под линией — марка потолка (план потолков)
- мебель и дверные проёмы за секущей плоскостью; число — марка и верх от чистого пола, мм

### Примечания

1. Разрезы — по линиям 1–1, 2–2 на плане потолков (лист 40). Отметки — от ±0,000 чистого пола, м; размеры — мм.
2. Высоты мебели и дверных блоков за секущей плоскостью сверены с низом потолка над ними: верх ниже низа короба и поля.
3. ГКЛ 12,5 мм по каркасу П113.
4. Толщины плит перекрытия и пирога пола показаны условно.
5. Ведомость объёмов потолков (лист ГКЛ, профиль, подвесы, лента, блоки питания, люки) — на листе 42.
6. Фрагменты 1, 2 — помещения с фигурными уровнями (размеры фигур, радиусы, отметки) — на листе 42.

1000 мм · печать 1:1

**Допущения и предложения на листе**

Основа листа: размеры сняты с плана заказчика, контрольный обмер не выполнен (К-5); высота потолка 2700 мм принята: на плане заказчика не указана (К-5); подрайон климата не задан — принят не северный (жилые от 2,5 м) (К-4); толщины стен приняты: наружные 250 мм, перегородки 120 мм — не обмерены (К-5); разрешённая мощность 15 кВт принята по типовой квартире, технических условий нет (К-6).
См. лист открытых вопросов (лист 6, записи К-4–К-6).

| Изм. | Кол.уч | Лист | № док. | Подп. | Дата |
|---|---|---|---|---|---|
| Разраб. | | Кырлан А.С. | | | 04.11.26 |
| Пров. | | | | | |
| ГИП | | | | | |
| | | | | | |
| Н. контр. | | | | | |
| Утв. | | | | | |

**ГД-2026-006-АИ**

Квартира 58 м²

Общая площадь 55,23* м² · * размеры приняты, не замерены (реестр — л. 6, 7, К-5)

Дизайн-проект интерьера

| Стадия | Лист | Листов |
|---|---|---|
| РП | 41 | 87 |

**Разрезы и узлы потолков**

М 1:40


**Кырлан Александр Сергеевич**

# Разрезы и узлы потолков (продолжение)

Фрагменты фигурных уровней · ведомость объёмов · размеры в мм

## Фрагмент 1. Пом. 1 Кухня-гостиная — уровни потолка (М 1:50)

Цепочки — от чистых граней стен; отметки — низ уровня от ±0,000

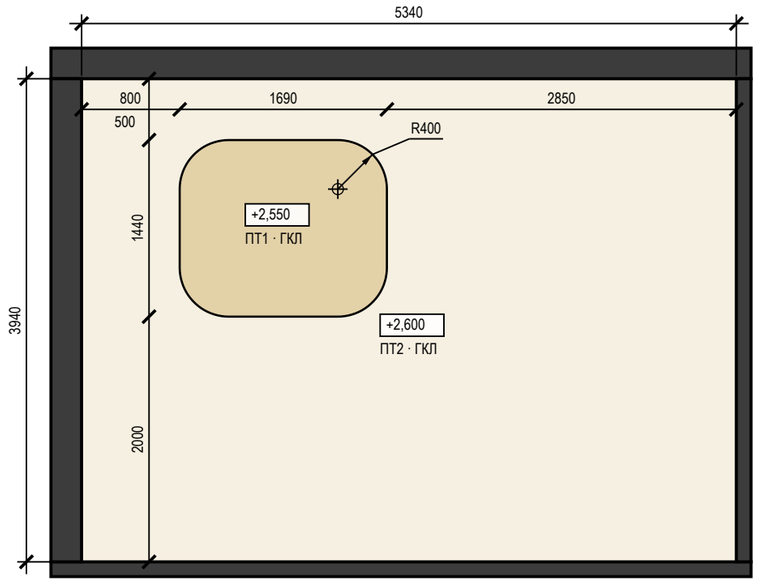



ПТ1 — низ +2,550

ПТ2 — низ +2,600

## Фрагмент 2. Пом. 2 Спальня — уровни потолка (М 1:50)

Цепочки — от чистых граней стен; отметки — низ уровня от ±0,000

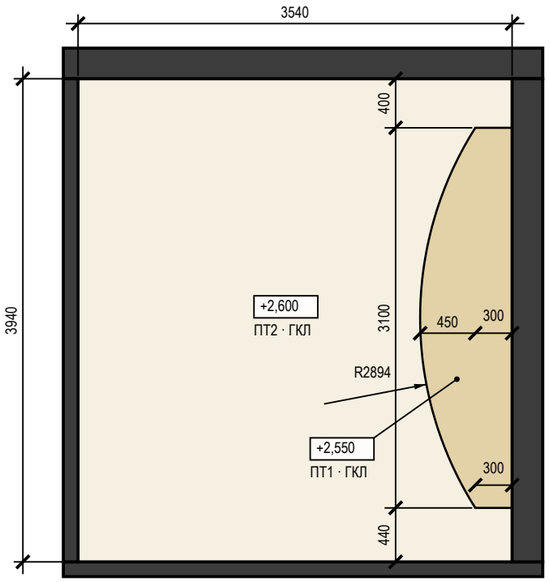


ПТ1 — низ +2,550

ПТ2 — низ +2,600

## Ведомость объёмов потолков

| Позиция | Ед. | Кол. | Пом. |
|---|---|---|---|
| Лист ГКЛ 12,5 | м² | 45,36 | 1, 2, 5 |
| Лист ГКЛВ 12,5 | м² | 4,75 | 3, 4 |
| Лист ГКЛ арочный 6,5 | м² | 0,25 | 1 |
| Борта и карнизы (входят в площади листов выше) | м² | 0,95 | 1, 2, 5 |
| Профиль ПП 60×27 | м | 142,49 | 1, 2, 3, 4, 5 |
| Профиль ПН 28×27 | м | 97,53 | 1, 2, 3, 4, 5 |
| Подвес прямой | шт. | 55 | 1, 2, 3, 4, 5 |
| Анкер-клин к плите | шт. | 55 | 1, 2, 3, 4, 5 |
| Шуруп TN 3,5×25 | шт. | 1156 | 1, 2, 3, 4, 5 |
| Лента армирующая для швов | м | 60,29 | 1, 2, 3, 4, 5 |
| Шпаклёвка для швов | кг | 20,10 | 1, 2, 3, 4, 5 |
| Грунтовка (швы) | л | 5,02 | 1, 2, 3, 4, 5 |
| Лента разделительная по периметру | м | 59,36 | 1, 2, 3, 4, 5 |
| Сплошная шпаклёвка и окраска (площадь развёртки) | м² | 50,24 | 1, 2, 3, 4, 5 |

**Допущения и предложения на листе**

Основа листа: размеры сняты с плана заказчика, контрольный обмер не выполнен (К-5); высота потолка 2700 мм принята: на плане заказчика не указана (К-5); подрайон климата не задан — принят не северный (жилые от 2,5 м) (К-4); толщины стен приняты: наружные 250 мм, перегородки 120 мм — не обмерены (К-5); разрешённая мощность 15 кВт принята по типовой квартире, технических условий нет (К-6).

См. лист открытых вопросов (лист 6, записи К-4–К-6).

## Примечания

1. ГКЛ 12,5 мм по каркасу П113; условные обозначения разрезов — на листе 41.
2. Фрагменты 1, 2 (план потолков — лист 40) — фигурные уровни потолка крупно: привязки краёв и центров фигур к чистым граням стен, радиусы (R) с центрами, хорда и стрелка дуги, отметки низа каждого уровня; цвета уровней — как на плане потолков.
3. Фигурные уровни: борт — ГКЛ по ПН с надрезами (на дуге шаг стоек борта 300 мм при R до 2500, 400 — до 5000) или по гнутому заводскому профилю (СП 163, 6.3.3); гибка: остров пом. 1 R400 — ГКЛ 6,5 мокрой гибкой; дуга пом. 2 R2894 — ГКЛ 12,5 сухой гибкой (СП 163, табл. 9).
4. Ведомость объёмов — по геометрии плана потолков: Лист ГКЛ 12,5 — плоскости уровней + борта (без арочных участков); Лист ГКЛВ 12,5 — плоскости уровней + борта; Лист ГКЛ арочный 6,5 — кривая борта × высота борта и стенки ниши × 2 слоя (R400 мокрая гибка); Борта и карнизы — длина перепада × перепад; Профиль ПП 60×27 — S × (1/шаг несущ. + 1/шаг осн.) + стойки бортов; Профиль ПН 28×27 — периметр стен + 2 × перепады + карнизы; Подвес прямой — по раскладке: S уровня / (шаг осн. × шаг подвесов), пояс уже шага — ряд вдоль пояса, фигура — по контуру; шаг подвесов — не больше табл. 14 СП 163; Анкер-клин к плите — по одному на подвес (Knauf П113); Шуруп TN 3,5×25 — 23 шт./м² (Knauf П113, табл. 2 альбома П 11); Лента армирующая для швов — 1,2 м/м² листа (Knauf); Шпаклёвка для швов — 0,4 кг/м² листа, только швы (Knauf); Грунтовка (швы) — 0,1 л/м² листа, только швы (Knauf); Лента разделительная по периметру — периметр стен под потолком ГКЛ; Сплошная шпаклёвка и окраска (площадь развёртки) — плоскости + борта; расход — по паспорту материала (норма расхода на сплошной слой не подтверждена); без запаса на подрезку (при закупке листа: ×1,075 при S > 20 м², ×1,175 — 10–20 м², ×1,275 — < 10 м²).

1000 мм · печать 1:1

| Изм. | Кол.уч | Лист | № док. | Подп. | Дата |
|---|---|---|---|---|---|
| Разраб. | | Кырлан А.С. | | | 04.11.26 |
| Пров. | | | | | |
| ГИП | | | | | |
| Н. контр. | | | | | |
| Утв. | | | | | |

**ГД-2026-006-АИ**

Квартира 58 м²

Общая площадь 55,23* м² · * размеры приняты, не замерены (реестр — л. 6, 7, К-5)

Дизайн-проект интерьера

| Стадия | Лист | Листов |
|---|---|---|
| РП | 42 | 87 |

**Разрезы и узлы потолков (продолжение)**

М 1:50

**Кырлан Александр Сергеевич**


выпуск 04.11.2026 № 3da8f16a26 · стр. 48 из 96

# Раскладка плитки. Планы полов


Раскладка от чистовых размеров · размеры в мм · отметки от ±0,000

ПРЕДВАРИТЕЛЬНО · не для производства работ · открыто пунктов: 10 (реестр — л. 6, 7)

**Фрагмент 1. Ванная (пом. 3). Пол 600×600, шов 2 мм, М 1:20**

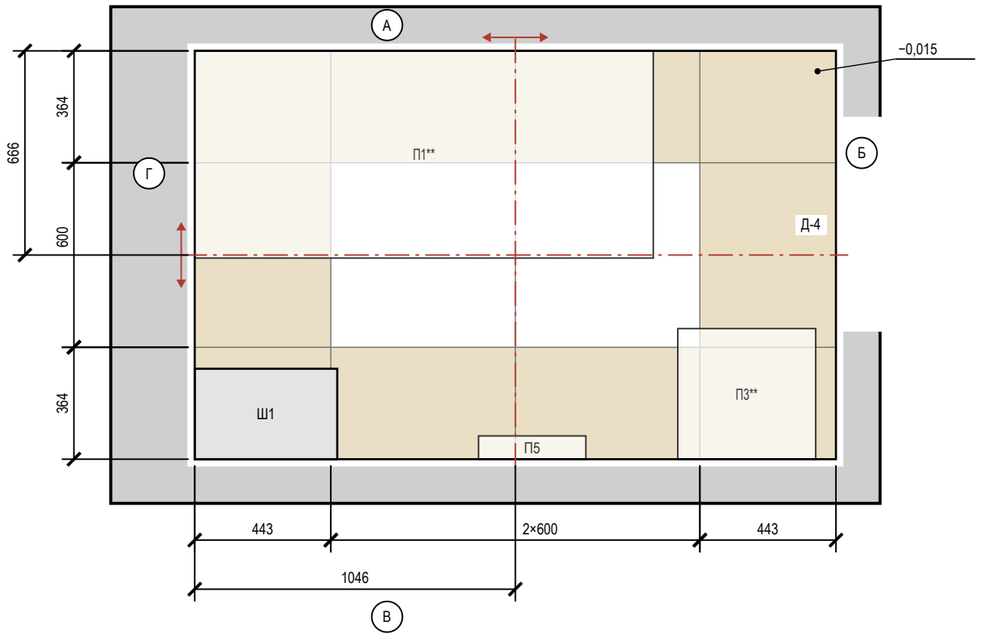


**Фрагмент 2. Санузел (пом. 4). Пол 600×600, шов 2 мм, М 1:20**

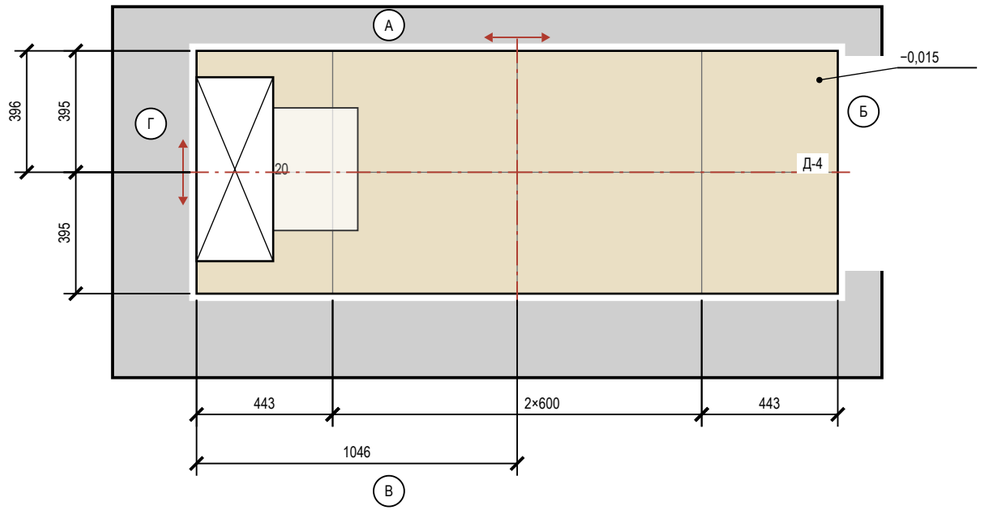


## Ведомость материалов

| Материал | Класс, код | Норма расхода | Кол-во |
|---|---|---|---|
| Затирка | класс не задан | (a+b)/ab·шов·t·1,6 | 3,9 кг |
| Клей | C2 S1 | 1,5 кг/м²·мм, слой 5 | 35 кг (2 меш.) |
| Клей | C2 | 1,5 кг/м²·мм, слой 5 | 332 кг (14 меш.) |
| Гидроизоляция | обмазочная, 2 слоя: пол, стены по периметру и зоны замачивания | по ТУ | 13,4 м² |
| Демпф. лента | по периметру пола из плитки | | 21,0 м |

## Ведомость плитки

| Помещение, поверхность | Плитка, код | Формат | Шов | S, м² | Целых | Подр. | С запасом |
|---|---|---|---|---|---|---|---|
| Ванная, пол | SG651622R | 600×600 | 2 | 2,95 | 2 | 10 | 14 |
| Ванная, стены А–Г | 610015000370 | 1200×600 | 2 | 14,95 | 0 | 40 | 44 |
| Ванная, короб стояков Ш1 489×319 | 610015000370 | 1200×600 | 2 | 1,99 | 0 | 10 | 12 |
| Санузел, пол | SG651622R | 600×600 | 2 | 1,80 | 0 | 8 | 9 |
| Санузел, стены А–Г | 610015000370 | 1200×600 | 2 | 13,40 | 0 | 30 | 34 |
| Санузел, короб инсталляции | 610015000370 | 1200×600 | 2 | 1,47 | 0 | 7 | 8 |
| Прихожая, пол | SG651622R | 600×600 | 2 | 9,55 | 10 | 18 | 31 |
| Итого 600×600 | | | | 14,30 | 12 | 36 | 54 |
| **Итого 600×1200** | | | | **31,80** | **0** | **87** | **98** |

## Условные обозначения

- плитка целая; тонкая линия — шов
- плитка с подрезкой (размер — на цепочке)
- ось старта; стрелки — направление укладки
- сантехприбор: габарит, высота по практике
- короб инсталляции: плитка пола — до короба
- короб стояков (Ш…): плитка пола — до короба
- отметка чистого пола на полке выноски, м
- (А) обозначение стены А–Г (как на развёртках)

## Примечания

1. Раскладка от чистовых размеров: стены санузлов теряют 10 + 5 + 9 = 24 мм на сторону (штукатурка, клей, плитка); подрезки чистые, без шва.
2. Старт — от центра помещения (штрихпунктир, стрелки направление укладки); размер старта — от чистовых стен Г и А.
3. Раскладка пола «Прихожая» — на листе «Раскладка плитки. Прихожая».
4. Калибр партии не задан — до укладки замерить (рабочий размер W, ГОСТ 13996-2019) и пересчитать подрезки.
5. Количество: целые по раскладке + по одной на подрезку, запас 10 %; один артикул — одна партия и тон. Исключены поддон, короб, проёмы и места за коробом; S — по чистым граням: стены нетто = зона облицовки по ведомости отделки − место за коробом инсталляции 2,71 м² (плитку за коробом не кладут), короб отдельной строкой.
6. Клей C2 S1; C2 (ГОСТ Р 56387-2018), затирка класс не задан; расход — по ТУ выбранной марки.
7. Гидроизоляция: пол и стены 200 мм от ЧП; над ванной — до 2000 и 300 мм за борт (пом. 3) (см. развёртки); акт скрытых работ, пролив 24 ч.
8. Отметка чистого пола −0,015, порог 15 мм; стык с соседним покрытием — по оси полотна двери.

**Допущения и предложения на листе**

Основа листа: размеры сняты с плана заказчика, контрольный обмер не выполнен (К-5); высота потолка 2700 мм принята: на плане заказчика не указана (К-5); подрайон климата не задан — принят не северный (жилые от 2,5 м) (К-4); толщины стен приняты: наружные 250 мм, перегородки 120 мм — не обмерены (К-5); разрешённая мощность 15 кВт принята по типовой квартире, технических условий нет (К-6).

Знак «**» — предложение проектировщика, заказчиком не утверждено (согласовать с заказчиком): К-2: П1 — ванна 1500 вместо 1600 — не заходит в проход перед проёмом Д-4; перед ванной 680 мм — глубина помещения; ПЗ — умывальник у стены В справа от ванны — перед ним свободно 750 мм, до стены Б 90 мм.

См. лист открытых вопросов (лист 6, записи К-2, К-4–К-6).

1000 мм · печать 1:1

| Изм. | Кол.уч | Лист | № док. | Подп. | Дата |
|---|---|---|---|---|---|
| Разраб. | | Кырлан А.С. | | | 04.11.26 |
| Пров. | | | | | |
| ГИП | | | | | |
| | | | | | |
| Н. контр. | | | | | |
| Утв. | | | | | |

**ГД-2026-006-АИ**

Квартира 58 м²

Общая площадь 55,23* м² · * размеры приняты, не замерены (реестр — л. 6, 7, К-5)

Дизайн-проект интерьера

| Стадия | Лист | Листов |
|---|---|---|
| РП | 43 | 87 |

**Раскладка плитки. Планы полов**

М 1:20

**Кырлан Александр Сергеевич**


выпуск 04.11.2026 № 3da8f16a26 · стр. 49 из 96

# Раскладка плитки. Прихожая

Раскладка от чистовых размеров · размеры в мм · высоты фартука от чистого пола

**ПРЕДВАРИТЕЛЬНО · не для производства работ · открыто пунктов: 10 (реестр — л. 6, 7)**

**Фрагмент 1. Прихожая (пом. 5). Пол 600×600, шов 2 мм, М 1:20**

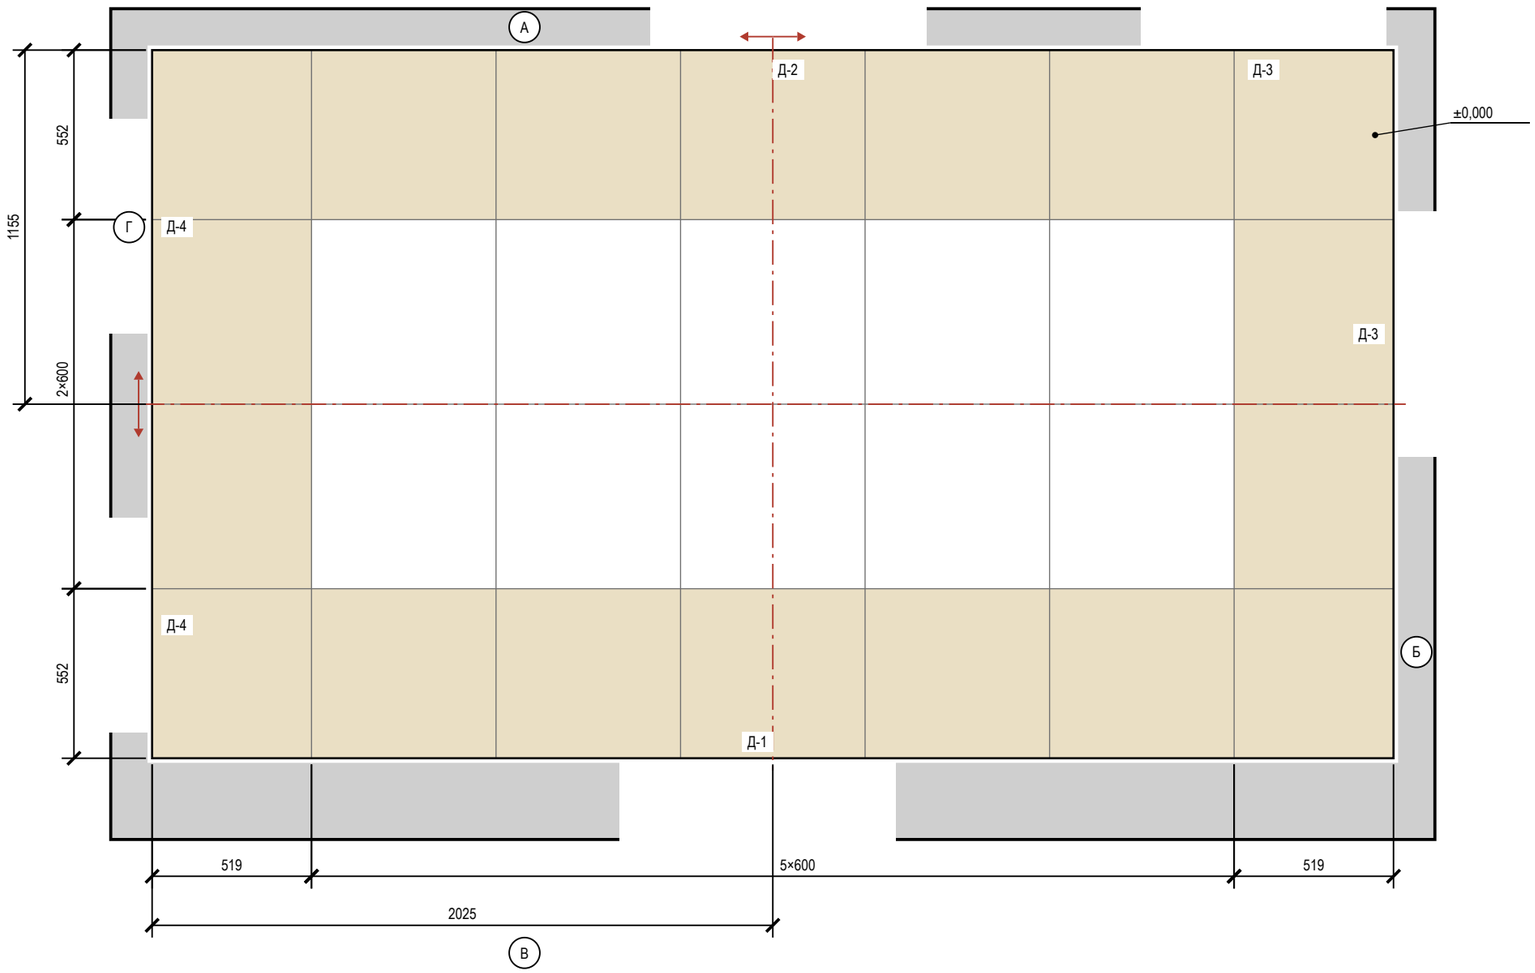


## Условные обозначения

- плитка целая; тонкая линия — шов
- плитка с подрезкой (размер — на цепочке)
- ось старта; стрелки — направление укладки
- отметка чистого пола на полке выноски, м
- (А) обозначение стены А–Г (как на развёртках)

## Подсчёт плитки

| Поверхность | Формат | S, м² | Целых | Подр. | С запасом |
|---|---|---|---|---|---|
| Прихожая, пол | 600×600 | 9,55 | 10 | 18 | 31 |

## Примечания

1. Прихожая: керамогранит 600×600, длинная сторона — вдоль стен Б и Г, шов 2 мм, прямая раскладка от центра. Стены окрашены: раскладка от чистового контура минус штукатурка и шпаклёвка 15 мм на сторону (принято); подрезки 519 / 552 мм, срез — под плинтус.
2. Прихожая: деформационный зазор по периметру 8–10 мм под плинтусом; в проёмах — стык с соседним покрытием по оси полотна двери. Клей С2, затирка класс не задан.
3. Клей, затирка и итог по форматам — в ведомостях листа «Раскладка плитки. Планы полов».

**Допущения и предложения на листе**

Основа листа: размеры сняты с плана заказчика, контрольный обмер не выполнен (К-5); высота потолка 2700 мм принята: на плане заказчика не указана (К-5); подрайон климата не задан — принят не северный (жилые от 2,5 м) (К-4); толщины стен приняты: наружные 250 мм, перегородки 120 мм — не обмерены (К-5); разрешённая мощность 15 кВт принята по типовой квартире, технических условий нет (К-6).

См. лист открытых вопросов (лист 6, записи К-4–К-6).

1000 мм · печать 1:1

| Изм. | Кол.уч | Лист | № док. | Подп. | Дата |
|---|---|---|---|---|---|
| Разраб. | | Кырлан А.С. | | | 04.11.26 |
| Пров. | | | | | |
| ГИП | | | | | |
| | | | | | |
| Н. контр. | | | | | |
| Утв. | | | | | |

**ГД-2026-006-АИ**

Квартира 58 м²

Общая площадь 55,23* м² · * размеры приняты, не замерены (реестр — л. 6, 7, К-5)

Дизайн-проект интерьера

| Стадия | Лист | Листов |
|---|---|---|
| РП | 44 | 87 |

**Раскладка плитки. Прихожая**


М 1:20

**Кырлан Александр Сергеевич**

# Раскладка плитки. Ванная. Развёртки стен

ПРЕДВАРИТЕЛЬНО · не для производства работ · открыто пунктов: 10 (реестр — л. 6, 7)

Пом. 3 · вид изнутри помещения · размеры в мм · высоты от чистого пола, отметки от ±0,000

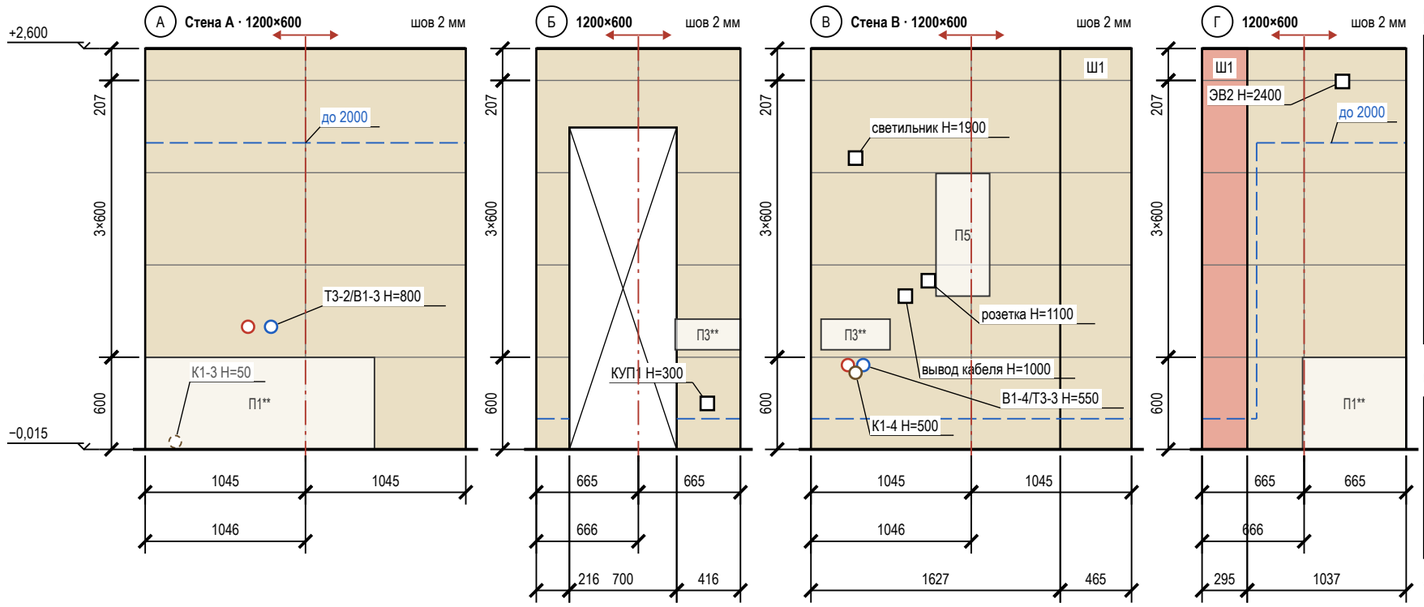


## Подсчёт плитки по стенам и коробу

| Поверхность | L × H, мм | S, м² | Целых | Подр. | С запасом | Подрезки: край / верх, мм |
|---|---|---|---|---|---|---|
| стена А | 2092 × 2615 | 5,60 | 0 | 10 | 11 | 1045 / 1045; 207 |
| стена Б | 1332 × 2615 | 2,14 | 0 | 10 | 11 | 665 / 665; 207 |
| стена В | 2092 × 2615 | 4,38 | 0 | 10 | 11 | 1045 / 1045; 207 |
| Ш1 489×319, ст. В | 465 × 2615 | 1,22 | 0 | 5 | 6 | лицо 465 |
| стена Г | 1332 × 2615 | 2,84 | 0 | 10 | 11 | 665 / 665; 207 |
| Ш1 489×319, ст. Г | 295 × 2615 | 0,77 | 0 | 5 | 6 | лицо 295 |
| **Итого** | | **16,94** | **0** | **50** | **56** | |

## Сдвиг точек под раскладку

| Точка (ВК, ЭОМ) | Стена | Проект: от угла / Н | Под раскладку: от угла / Н | Сдвиг, мм |
|---|---|---|---|---|
| розетка | В | 766 / 1100 | 766 / 1203 | Н +103 |
| вывод кабеля | В | 616 / 1000 | 616 / 902 | Н −98 |
| светильник | В | 291 / 1900 | 291 / 1805 | Н −95 |

## Условные обозначения

- плитка целая; тонкая линия — шов
- плитка с подрезкой (размер — на цепочке)
- ось старта; стрелки — направление укладки
- верх гидроизоляции: 200 от ЧП, в мокрой зоне — «до …»
- проём — не облицовывается
- сантехприбор: габарит, высота по практике
- грань короба стояков (Ш…): своя сетка, за коробом плитку не кладут
- вывод В1 (код — в ведомости привязок)
- вывод Т3 (код — в ведомости привязок)
- вывод К1 (код — в ведомости привязок)
- вывод за прибором / в коробе (не на сетке)
- электроточка: марка и Н — по листам ЭОМ
- отметка уровня, м: ±0,000 — чистый пол жилых помещений
- низ потолка; серая полоса — стена без плитки
- (А) обозначение стены А–Г (как на развёртках)

## Примечания

1. Вид изнутри, стены по часовой стрелке А → Г. Высоты — от чистого пола (−0,015), отметки — от ±0,000. Раскладка от чистовых размеров (штукатурка 10 + клей 5 + плитка 9 мм), подрезки чистые; старт — от оси стены, ряды от пола целыми.
2. Облицовка до потолка (+2,600).
3. Точки из таблицы сдвигов переносятся до черновой разводки (ЭОМ — по тем же числам).
4. Выводы ВК стоят по оси прибора и с прибором не двигаются — привязки по «Плану выводов сантехники» без сдвига; вне сетки (Т3-2/В1-3, В1-4/Т3-3, К1-4) отверстие в плитке коронкой по той же привязке, плитку не сдвигать.
5. Выводы — по «Плану выводов сантехники», электроточки — по ЭОМ, «*» — высота по практике; за приборами и в коробе (К1-3) — штриховым кольцом.
6. Гидроизоляция: 200 мм от ЧП по периметру; над ванной — до 2000 и 300 мм за борт (СП 29.13330.2011, п. 7.2 — на высоту замачивания); углы — лентой; акт скрытых работ, пролив.
7. Короб стояков Ш1: грани 465 мм (ст. В), 295 мм (ст. Г) — плиткой стен по рядам стены, целая плитка от наружного угла; угол — запил 45° или профиль; за коробом плитку не кладут. Люк 300×400 — на грани ст. В: высота — по месту ревизии стояка (положение стояков сверяется на объекте), кромки дверцы по швам сетки, дверца нажимная под плитку.

**Допущения и предложения на листе**

Основа листа: размеры сняты с плана заказчика, контрольный обмер не выполнен (К-5); высота потолка 2700 мм принята: на плане заказчика не указана (К-5); подрайон климата не задан — принят не северный (жилые от 2,5 м) (К-4); толщины стен приняты: наружные 250 мм, перегородки 120 мм — не обмерены (К-5); разрешённая мощность 15 кВт принята по типовой квартире, технических условий нет (К-6).

Знак «**» — предложение проектировщика, заказчиком не утверждено (согласовать с заказчиком): К-2: П1 — ванна 1500 вместо 1600 — не заходит в проход перед проёмом Д-4; перед ванной 680 мм — глубина помещения; П3 — умывальник у стены В справа от ванны — перед ним свободно 750 мм, до стены Б 90 мм.

См. лист открытых вопросов (лист 6, записи К-2, К-4–К-6).

1000 мм · печать 1:1

| Изм. | Кол.уч | Лист | № док. | Подп. | Дата |
|---|---|---|---|---|---|
| Разраб. | | Кырлан А.С. | | | 04.11.26 |
| Пров. | | | | | |
| ГИП | | | | | |
| | | | | | |
| Н. контр. | | | | | |
| Утв. | | | | | |

**ГД-2026-006-АИ**

Квартира 58 м²

Общая площадь 55,23* м² · * размеры приняты, не замерены (реестр — л. 6, 7, К-5)

Дизайн-проект интерьера

| Стадия | Лист | Листов |
|---|---|---|
| РП | 45 | 87 |

**Раскладка плитки. Ванная. Развёртки стен**

М 1:40


**Кырлан Александр Сергеевич**

выпуск 04.11.2026 № 3da8f16a26 · стр. 51 из 96

# Раскладка плитки. Санузел. Развёртки стен

ПРЕДВАРИТЕЛЬНО · не для производства работ · открыто пунктов: 10 (реестр — л. 6, 7)

Пом. 4 · вид изнутри помещения · размеры в мм · высоты от чистого пола, отметки от ±0,000

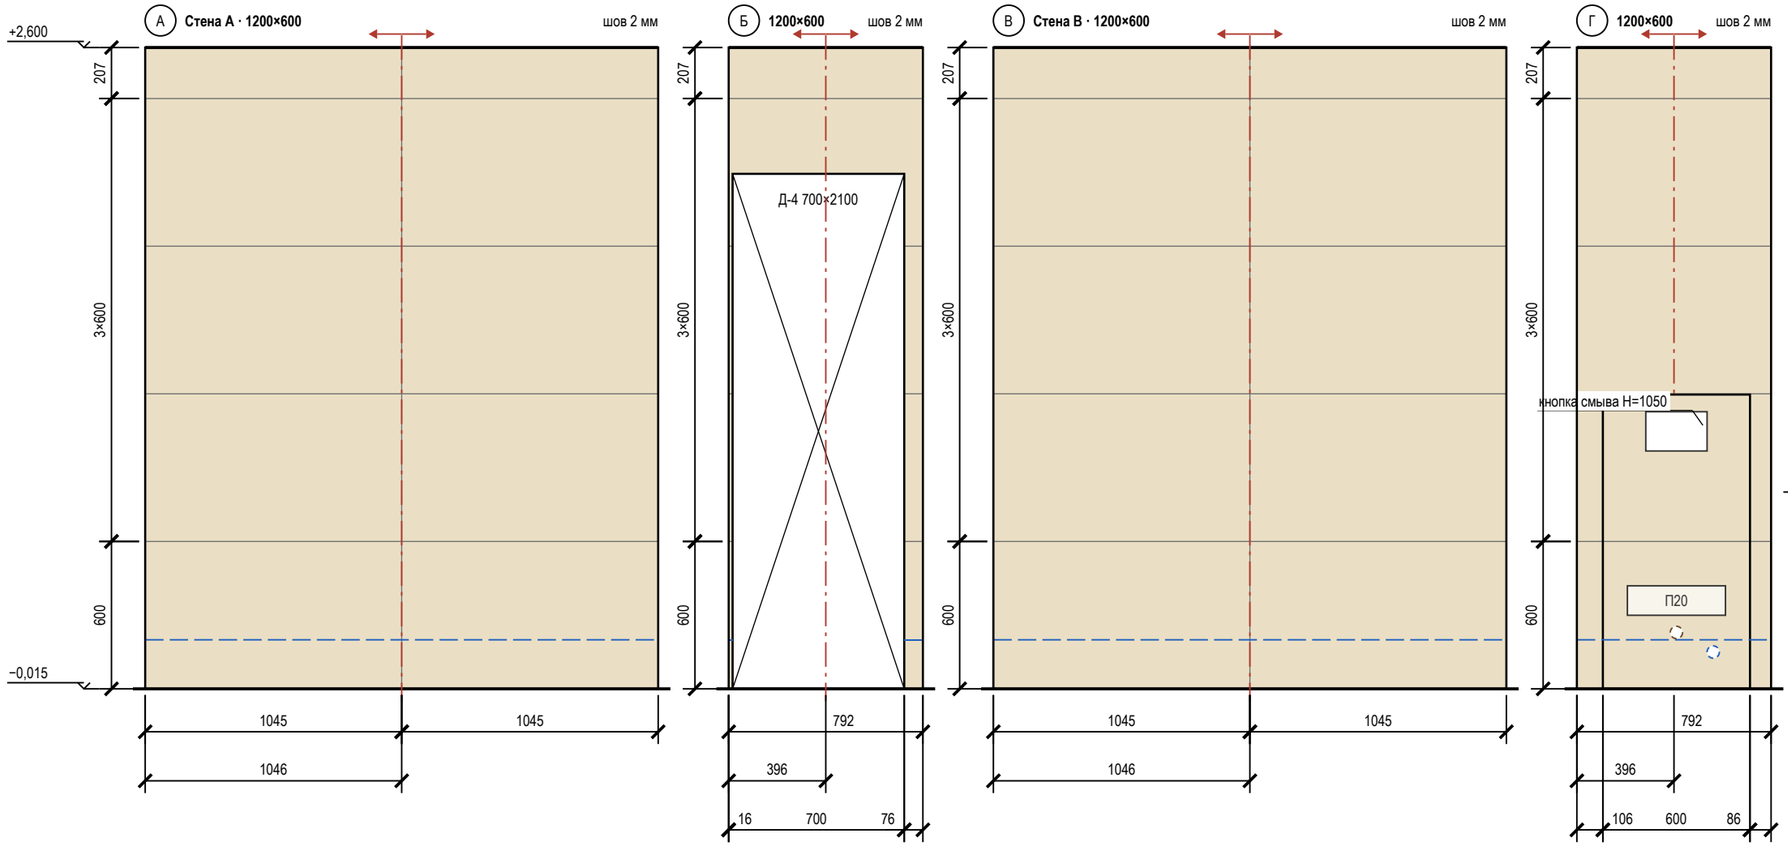


## Условные обозначения

- плитка целая; тонкая линия — шов
- плитка с подрезкой (размер — на цепочке)
- ось старта; стрелки — направление укладки
- верх гидроизоляции: 200 от ЧП, в мокрой зоне — «до …»
- проём — не облицовывается
- сантехприбор: габарит, высота по практике
- короб инсталляции, в нём кнопка смыва 250×160
- вывод В1 (код — в ведомости привязок)
- вывод К1 (код — в ведомости привязок)
- вывод за прибором / в коробе (не на сетке)
- отметка уровня, м: ±0,000 — чистый пол жилых помещений
- низ потолка; серая полоса — стена без плитки
- А — обозначение стены А–Г (как на развёртках)

## Подсчёт плитки по стенам и коробу

| Поверхность | L × H, мм | S, м² | Целых | Подр. | С запасом | Подрезки: край / верх, мм |
|---|---|---|---|---|---|---|
| стена А | 2092 × 2615 | 5,60 | 0 | 10 | 11 | 1045 / 1045; 207 |
| стена Б | 792 × 2615 | 0,73 | 0 | 5 | 6 | 792; 207 |
| стена В | 2092 × 2615 | 5,60 | 0 | 10 | 11 | 1045 / 1045; 207 |
| стена Г | 792 × 2615 | 1,48 | 0 | 5 | 6 | 792; 207 |
| короб (ст. Г) | 600×1200×250 | 1,47 | 0 | 7 | 8 | лицо 600; бок. 250 |
| **Итого** | | **14,87** | **0** | **37** | **42** | |

## Примечания

1. Вид изнутри, стены по часовой стрелке А → Г. Высоты — от чистого пола (−0,015), отметки — от ±0,000. Раскладка от чистовых размеров (штукатурка 10 + клей 5 + плитка 9 мм), подрезки чистые; старт — от оси стены, ряды от пола целыми.
2. Облицовка до потолка (+2,600).
3. Открытые выводы и электроточки — на шве или в центре плитки (допуск 10 мм; плитка от 900 мм по высоте — на шве или не ближе 60 мм к нему).
4. Выводы — по «Плану выводов сантехники», электроточки — по ЭОМ, «*» — высота по практике; за приборами и в коробе (В1-5, К1-5) — штриховым кольцом.
5. Гидроизоляция: 200 мм от ЧП по периметру; углы — лентой; акт скрытых работ, пролив.
6. Короб 600×1200×250: лицо 600 мм от оси кнопки смыва, боковины, полка; углы — запил 45° или профиль; за коробом плитку не кладут.
7. Между коробом и углом полоса 86 и 106 мм — довести короб до угла.

**Допущения и предложения на листе**

Основа листа: размеры сняты с плана заказчика, контрольный обмер не выполнен (К-5); высота потолка 2700 мм принята: на плане заказчика не указана (К-5); подрайон климата не задан — принят не северный (жилые от 2,5 м) (К-4); толщины стен приняты: наружные 250 мм, перегородки 120 мм — не обмерены (К-5); разрешённая мощность 15 кВт принята по типовой квартире, технических условий нет (К-6).

См. лист открытых вопросов (лист 6, записи К-4–К-6).

1000 мм · печать 1:1

| Изм. | Кол.уч | Лист | № док. | Подп. | Дата |
|---|---|---|---|---|---|
| Разраб. | | Кырлан А.С. | | | 04.11.26 |
| Пров. | | | | | |
| ГИП | | | | | |
| | | | | | |
| Н. контр. | | | | | |
| Утв. | | | | | |

**ГД-2026-006-АИ**

Квартира 58 м²

Общая площадь 55,23* м² · * размеры приняты, не замерены (реестр — л. 6, 7, К-5)

| Дизайн-проект интерьера | Стадия | Лист | Листов |
|---|---|---|---|
| | РП | 46 | 87 |

**Раскладка плитки. Санузел. Развёртки стен**

М 1:25

**Кырлан Александр Сергеевич**

выпуск 04.11.2026 № 3da8f16a26 · стр. 52 из 96

07

# Полы и отделка

Кырлан Александр Сергеевич

выпуск 04.11.2026 · 3da8f16a26 · стр. 53 из 96

# План полов

Покрытия, направление укладки, отметки чистого пола, стыки · размеры в мм · отметки в м


**ПРЕДВАРИТЕЛЬНО · не для производства работ · открыто пунктов: 10 (реестр — л. 6, 7)**

## Условные обозначения

- тип 1 — инженерная доска, линии — вдоль доски
- тип 2 — керамогранит 600×600, сетка — формат плитки
- тип 3 — керамогранит 600×600, сетка — формат плитки
- номер типа пола (экспликация полов)
- схема пола, без масштаба: плита — штриховка, стяжка — точки, звукоизоляция — зигзаг, гидроизоляция — утолщённая линия с заведением на стену
- направление укладки (длинная сторона доски)
- отметка чистого пола, м
- стык в проёме: решение не задано
- стык в проёме: порог
- СТ1 — марка стыка (ведомость стыков)
- стояк: К1 — канализация, В1 ХВС, Т3 — ГВС
- 1 — номер помещения, площадь м²

## Отметки по высоте

| | |
|---|---|
| **±0,000** | чистый пол пом. 1, 2, 5, 6; отсчёт высот |
| **−0,015** | чистый пол пом. 3, 4, ниже на 15 мм |
| **−0,064*** | верх плиты — расчёт, не замер (задание на обмер) |
| **сущ. пол** | снимается до плиты; не замерен (задание на обмер) |

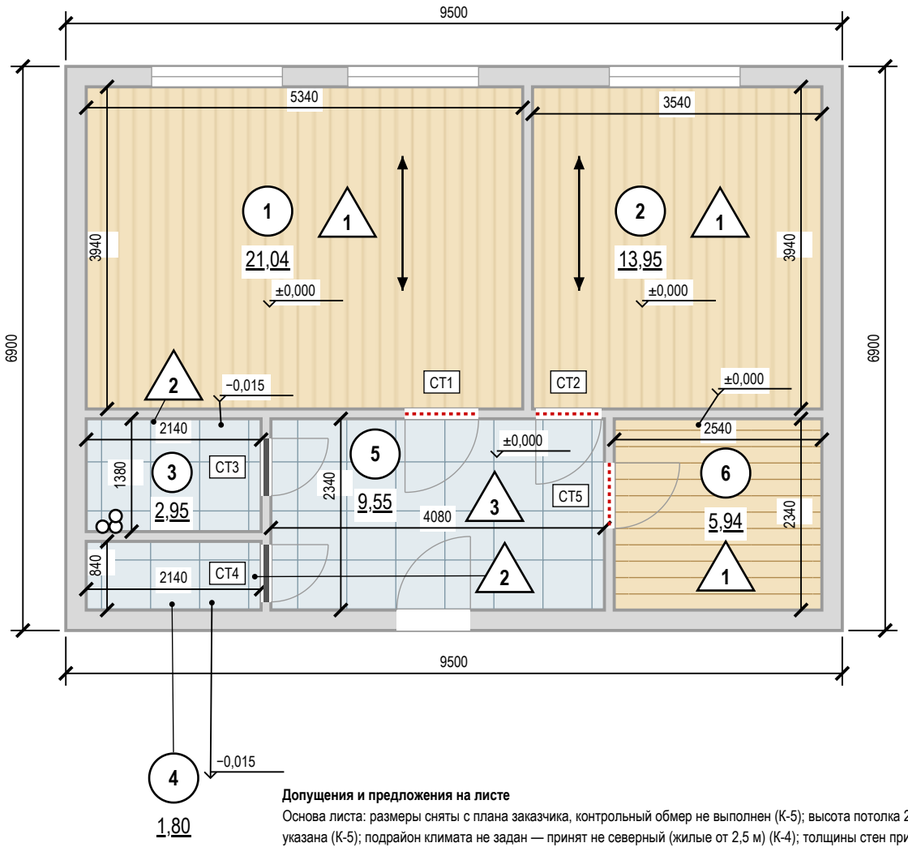





**Допущения и предложения на листе**

Основа листа: размеры сняты с плана заказчика, контрольный обмер не выполнен (К-5); высота потолка 2700 мм принята: на плане заказчика не указана (К-5); подрайон климата не задан — принят не северный (жилые от 2,5 м) (К-4); толщины стен приняты: наружные 250 мм, перегородки 120 мм — не обмерены (К-5); разрешённая мощность 15 кВт принята по типовой квартире, технических условий нет (К-6).

Знак «**» — предложение проектировщика, заказчиком не утверждено (согласовать с заказчиком): пол пом. 1, 2, 6 — артикул изделия не выбран: позиция описана характеристиками («аналог по характеристикам»), артикул выбирается при закупке.

См. лист открытых вопросов (лист 6, записи К-4–К-6).

## Экспликация полов
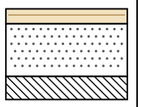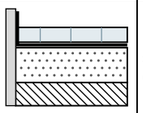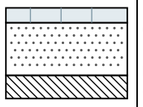
| Номер помещения | Тип пола | Схема пола | Данные элементов пола (наименование, толщина, основание), мм | Площадь, м² |
|---|---|---|---|---|
| 1, 2, 6 | 1 |  | Инженерная доска на клею — 14<br>Стяжка ЦПС М200 — 50<br>Плита перекрытия<br>Всего 64 мм; ЧП ±0,000, верх плиты −0,064 | 40,93 |
| 3, 4 | 2 |  | Керамогранит на клею С2 TE S1 — 14<br>Гидроизоляция обмазочная, 2 слоя, с заведением на стены 200 мм — 2<br>Стяжка ЦПС М200 — 33<br>Плита перекрытия<br>Всего 49 мм; ЧП −0,015, верх плиты −0,064 | 4,75 |
| 5 | 3 |  | Керамогранит на клею С2 TE S1 — 14<br>Стяжка ЦПС М200 — 50<br>Плита перекрытия<br>Всего 64 мм; ЧП ±0,000, верх плиты −0,064 | 9,55 |
| | | | **Итого** | **55,23** |

## Раскладка покрытий

| Пом. | Укладка | Старт (оси от чистовых стен), мм | Отступ 1-го ряда / крайние плитки, мм |
|---|---|---|---|
| 1 | вдоль стен Б/Г, прямая | от стены Г, 1-й ряд вдоль неё | зазор от стены не задан |
| 2 | вдоль стен Б/Г, прямая | от стены Г, 1-й ряд вдоль неё | зазор от стены не задан |
| 3 | плитка | раскладка плиточника не задана | |
| 4 | плитка | раскладка плиточника не задана | |
| 5 | плитка | раскладка плиточника не задана | |
| 6 | вдоль стен А/В, прямая | от стены А, 1-й ряд вдоль неё | зазор от стены не задан |

## Стыки покрытий в проёмах

| Марка | Проём | Типы пола | Отметки ЧП | Решение |
|---|---|---|---|---|
| СТ1 | 5–1 (Д-2) | 3 / 1 | ±0,000 / ±0,000 | не задано |
| СТ2 | 5–2 (Д-3) | 3 / 1 | ±0,000 / ±0,000 | не задано |
| СТ3 | 5–3 (Д-4) | 3 / 2 | ±0,000 / −0,015 | порог h=15 мм |
| СТ4 | 5–4 (Д-4) | 3 / 2 | ±0,000 / −0,015 | порог h=15 мм |
| СТ5 | 6–5 (Д-3) | 1 / 3 | ±0,000 / ±0,000 | не задано |

## Примечания

1. За отметку ±0,000 принят чистый пол, не существующий (блок отметок). Площади — по чистым размерам помещений, м²; размеры — в мм.
2. Стык разнотипных покрытий — по оси дверного полотна (под полотном в закрытом положении); решение стыка — по ведомости стыков.
3. Пол санузлов ниже смежных помещений на 15 мм за счёт меньшей толщины стяжки (верх плиты общий — по экспликации полов); гидроизоляция по стяжке с заведением на стены не менее 200 мм (СП 29.13330.2011, п. 7.2), до облицовки — тест проливом и акт скрытых работ.
4. Трубопроводы в конструкции пола не прокладываются: пирог пола 49–64 мм не вмещает выпуски канализации с уклоном — выпуски К1 ведутся по стенам над чистым полом в коробах (лист 30).
5. Звукоизоляционный слой под стяжкой проектом не предусмотрен (стяжка по плите): приведённый уровень ударного шума перекрытия с полом Lnw не более 60 дБ (СП 51.13330.2011, табл. 2) подтвердить по данным дома; при превышении — плавающая стяжка по звукоизоляции с демпферной лентой по контуру и у стояков, пирог пересчитать.
6. Штучные покрытия (инженерная доска): направление — по стрелке; влажность основания по СМ не более 2,0 % (по ТУ изготовителя).
7. Ровность основания — просвет под 2-метровой рейкой не более 2 мм: пом. 1, 2, 6 (инженерная доска), пом. 3, 4, 5 (керамогранит); проверить до укладки покрытия (СП 71.13330.2017, табл. 8.5).
8. Сетка на плитке — условная, в размер формата; точка старта и раскладка — по листу раскладки плитки.
9. Узор покрытия (заливка-код типа пола) прерывается под надписями — площадями помещений и отметками чистого пола.
10. Пироги полов — по экспликации полов: слои сверху вниз, толщины в мм; гидроизоляция мокрых зон — в пироге и в ведомости отделки; схема пола — без масштаба.

1000 мм · печать 1:1

| Изм. | Кол.уч | Лист | № док. | Подп. | Дата |
|---|---|---|---|---|---|
| Разраб. | | Кырлан А.С. | | | 04.11.26 |
| Пров. | | | | | |
| ГИП | | | | | |
| | | | | | |
| Н. контр. | | | | | |
| Утв. | | | | | |

**ГД-2026-006-АИ**

Квартира 58 м²

Общая площадь 55,23* м² · * размеры приняты, не замерены (реестр — л. 6, 7, К-5)

Дизайн-проект интерьера

| Стадия | Лист | Листов |
|---|---|---|
| РП | 47 | 87 |

**План полов**

М 1:75

**Кырлан Александр Сергеевич**

выпуск 04.11.2026 № 3da8f16a26 · стр. 54 из 96

# Ведомость отделки помещений

Потолки, стены, низ стен, полы · площади в м², длины в м · отметки в м

## Ведомость отделки помещений (форма 1 прил. А ГОСТ 21.501-2018)

| № | Наименование помещения | Потолок | | | Стены и перегородки | | | Низ стен (плинтус) | | | Пол | | Примечание |
|---|---|---|---|---|---|---|---|---|---|---|---|---|---|
| | | Вид отделки | Код цвета | S, м² | Вид отделки | Код цвета | S, м² | Вид отделки | Код цвета | L, м | Вид отделки | S, м² | |
| 1 | Кухня-гостиная 21,04 м² | ГКЛ по каркасу П113, отм. +2,600; +2,550; окраска, Tikkurila, глубокоматовая | NCS S 0300-N | 21,04 | Окраска, Tikkurila, полуматовая, подготовка Q3 | NCS S 1002-Y50R | 41,25 | Плинтус МДФ h=110 мм, SX184 | NCS S 0300-N | 17,7 | Аналог: инженерная доска, дуб натуральный, масло, 1-полосная, 14/4 мм, на клею; тип 1, отм. ЧП ±0,000 | 21,04 | Н стен 2600 (до потолка) |
| 2 | Спальня 13,95 м² | ГКЛ по каркасу П113, отм. +2,600; +2,550; окраска, Tikkurila, глубокоматовая | NCS S 0300-N | 13,95 | Окраска, Tikkurila, глубокоматовая, подготовка Q3 | NCS S 1502-Y50R | 33,91 | Плинтус МДФ h=110 мм, SX184 | NCS S 0300-N | 14,2 | Аналог: инженерная доска, дуб натуральный, масло, 1-полосная, 14/4 мм, на клею; тип 1, отм. ЧП ±0,000 | 13,95 | Н стен 2550 (до потолка) |
| 3 | Ванная 2,95 м² | ГКЛВ по каркасу П113, отм. +2,600; окраска, Tikkurila, глубокоматовая | NCS S 0300-N | 2,95 | Облицовка плиткой, 610015000370, 600×1200 мм, клей С2 | Italon 610015000370 | 16,94 | нет (облицовка от пола) | | | Керамогранит, SG651622R, 600×600 мм; тип 2, отм. ЧП −0,015 | 2,95 | Н стен 2615 (до потолка); тёплый пол; гидроизоляция обмазочная, 2 слоя, с заведением на стены 200 мм; над ванной — до 2000 и 300 мм за борт (по пирогу пола); тест проливом и акт скрытых работ |
| 4 | Санузел 1,80 м² | ГКЛВ по каркасу П113, отм. +2,600; окраска, Tikkurila, глубокоматовая | NCS S 0300-N | 1,80 | Облицовка плиткой, 610015000370, 600×1200 мм, клей С2 | Italon 610015000370 | 14,12 | нет (облицовка от пола) | | | Керамогранит, SG651622R, 600×600 мм; тип 2, отм. ЧП −0,015 | 1,80 | Н стен 2615 (до потолка); гидроизоляция обмазочная, 2 слоя, с заведением на стены 200 мм (по пирогу пола); тест проливом и акт скрытых работ |
| 5 | Прихожая 9,55 м² | ГКЛ по каркасу П113, отм. +2,550; +2,600; окраска, Tikkurila, глубокоматовая | NCS S 0300-N | 9,55 | Окраска, Tikkurila, полуматовая, подготовка Q3 | NCS S 1502-Y50R | 22,66 | Плинтус МДФ h=110 мм, SX184 | NCS S 0300-N | 8,0 | Керамогранит, SG651622R, 600×600 мм; тип 3, отм. ЧП ±0,000 | 9,55 | Н стен 2550 (до потолка) |
| 6 | Гардеробная 5,94 м² | Существующий потолок, отм. +2,700; окраска, Tikkurila Anti-Reflex 2, глубокоматовая, 2 слоя, подготовка Q3 | Tikkurila V503 | 5,94 | Окраска, Tikkurila Harmony, матовая, 2 слоя, подготовка Q3 | Tikkurila V503 | 24,67 | Плинтус МДФ h=110 мм, SX184 | Tikkurila V503 | 9,0 | Аналог: инженерная доска, дуб натуральный, масло, 1-полосная, 14/4 мм, на клею; тип 1, отм. ЧП ±0,000 | 5,94 | Н стен 2700 (до потолка); плинтус в цвет: стены |
| | **Итого** | | | **55,23** | | | **153,54** | | | **48,8** | | **55,23** | |

### Сводка площадей по материалам отделки

| Поверхность | Материал / код цвета | Серия | Площадь, м² |
|---|---|---|---|
| Потолок | NCS S 0300-N | | 49,29 |
| Потолок | Tikkurila V503 | Anti-Reflex 2 | 5,94 |
| Стены | NCS S 1002-Y50R | | 41,25 |
| Стены | NCS S 1502-Y50R | | 56,57 |
| Стены | облицовка плиткой 600×1200 мм, Italon 610015000370 | 610015000370 | 31,05 |
| Стены | Tikkurila V503 | Harmony | 24,67 |

**Допущения и предложения на листе**

Основа листа: размеры сняты с плана заказчика, контрольный обмер не выполнен (К-5); высота потолка 2700 мм принята: на плане заказчика не указана (К-5); подрайон климата не задан — принят не северный (жилые от 2,5 м) (К-4); толщины стен приняты: наружные 250 мм, перегородки 120 мм — не обмерены (К-5); разрешённая мощность 15 кВт принята по типовой квартире, технических условий нет (К-6).

Знак «**» — предложение проектировщика, заказчиком не утверждено (согласовать с заказчиком): пол пом. 1, 2, 6 — артикул изделия не выбран: позиция описана характеристиками («аналог по характеристикам»), артикул выбирается при закупке.

См. лист открытых вопросов (лист 6, записи К-4–К-6).

## Примечания

1. Площади поверхностей — по чистым граням стен до отделки: стены = периметр × высоту от чистого пола помещения до низа потолка минус проёмы (облицовка плиткой — до верха облицовки); плинтус = периметр минус дверные проёмы; пол и потолок — по площади помещения. Количество плиток по раскладке. Площади помещений — с учётом всех частей помещения; откосы в площадь стен не входят.
2. Акцентные стены — отдельными строками, их площадь вычтена из основной отделки стен помещения.
3. Плинтус — длина по периметру за вычетом дверных проёмов; примыкания к наличникам и встроенной мебели — по развёрткам.
4. Формат плитки — Ш×В×Т (ширина × высота в положении укладки × толщина), мм; на полу — вдоль стен А/В × вдоль стен Б/Г.
5. Коды цвета — по веерам производителей; колеровка каждой краски одной партией, проверка выкраса при свете D65 и при лампах проекта.
6. Уровни подготовки Q1–Q4 — система Knauf, не норма ГОСТ/СП; допуски поверхностей — по СП 71.13330.2017 (действующая редакция).
7. «аналог:» — изделие задано характеристиками, марку и артикул согласовать с заказчиком до закупки.

| Изм. | Кол.уч | Лист | № док. | Подп. | Дата |
|---|---|---|---|---|---|
| Разраб. | | Кырлан А.С. | | | 04.11.26 |
| Пров. | | | | | |
| ГИП | | | | | |
| | | | | | |
| Н. контр. | | | | | |
| Утв. | | | | | |

**ГД-2026-006-АИ**

Квартира 58 м²

Общая площадь 55,23* м² · * размеры приняты, не замерены (реестр — л. 6, 7, К-5)

Дизайн-проект интерьера

| Стадия | Лист | Листов |
|---|---|---|
| РП | 48 | 87 |

**Ведомость отделки помещений**

М б/м

**Кырлан Александр Сергеевич**

# Колерная карта

Цвета и материалы по помещениям · палитра проекта · выкрасы на согласование


## Колерная карта по помещениям

| Помещение | Поверхность | Образец | Поз. | Система и код цвета | Производитель, линейка / материал, артикул | Блеск | Класс истирания | LRV | Площадь |
|---|---|---|---|---|---|---|---|---|---|
| **1. Кухня-гостиная** 21,04 м² | стены | | **К1** | NCS S 1002-Y50R | Tikkurila | полуматов. | 1 | 82 | 41,2 м² |
| | потолок | | **К2** | NCS S 0300-N | Tikkurila | глубокомат. | 1 | 92 | 21,0 м² |
| | пол | | **КМ1** | по образцу | инженерная доска · аналог по хар. | | | | 21,0 м² |
| | плинтус | | **К3** | NCS S 0300-N | Orac Decor · Luxxus | полуматов. | | 92 | 17,7 м |
| **2. Спальня** 13,95 м² | стены | | **К4** | NCS S 1502-Y50R | Tikkurila | глубокомат. | 2 | 72 | 33,9 м² |
| | потолок | | **К5** | NCS S 0300-N | Tikkurila | глубокомат. | 2 | 92 | 13,9 м² |
| | пол | | **КМ1** | по образцу | инженерная доска · аналог по хар. | | | | 13,9 м² |
| | плинтус | | **К3** | NCS S 0300-N | Orac Decor · Luxxus | полуматов. | | 92 | 14,2 м |
| **3. Ванная** 2,95 м² | стены | | **КМ2** | Charme Extra | Italon · арт. 610015000370 | | | | 16,9 м² |
| | потолок | | **К2** | NCS S 0300-N | Tikkurila | глубокомат. | 1 | 92 | 3,0 м² |
| | пол | | **КМ3** | Две Венеции / Риальто | Kerama Marazzi · арт. SG651622R | | | | 3,0 м² |
| **4. Санузел** 1,8 м² | стены | | **КМ2** | Charme Extra | Italon · арт. 610015000370 | | | | 14,1 м² |
| | потолок | | **К2** | NCS S 0300-N | Tikkurila | глубокомат. | 1 | 92 | 1,8 м² |
| | пол | | **КМ3** | Две Венеции / Риальто | Kerama Marazzi · арт. SG651622R | | | | 1,8 м² |
| **5. Прихожая** 9,55 м² | стены | | **К6** | NCS S 1502-Y50R | Tikkurila | полуматов. | 1 | 72 | 22,7 м² |
| | потолок | | **К2** | NCS S 0300-N | Tikkurila | глубокомат. | 1 | 92 | 9,6 м² |
| | пол | | **КМ3** | Две Венеции / Риальто | Kerama Marazzi · арт. SG651622R | | | | 9,6 м² |
| | плинтус | | **К3** | NCS S 0300-N | Orac Decor · Luxxus | полуматов. | | 92 | 8,0 м |
| **6. Гардеробная** 5,94 м² | стены | | **К7** | Tikkurila V503 | Tikkurila · Harmony | матовая | 1 | 86 | 24,7 м² |
| | потолок | | **К8** | Tikkurila V503 | Tikkurila · Anti-Reflex 2 | глубокомат. | 2 | 86 | 5,9 м² |
| | пол | | **КМ1** | по образцу | инженерная доска · аналог по хар. | | | | 5,9 м² |
| | плинтус | | **К9** | Tikkurila V503 | Orac Decor · Luxxus | | | 86 | 9,0 м |

## Перечень выкрасов на согласование

| № | Код | Бренд / веер | Пом. / стена | Подложка | Формат | Статус |
|---|---|---|---|---|---|---|
| 1 | S 1002-Y50R | NCS Tikkurila | 1 | ГКЛ с грунтом | 600×1000 | к выполнению |
| 2 | S 0300-N | NCS Tikkurila | 1, 2, 3, 4, 5 | ГКЛ с грунтом; МДФ под эмаль | 600×1000; 300×600 | к выполнению |
| 3 | S 1502-Y50R | NCS Tikkurila | 2, 5 | ГКЛ с грунтом | 600×1000 | к выполнению |
| 4 | V503 | Tikkurila | 6 | ГКЛ с грунтом; МДФ под эмаль | 600×1000; 300×600 | к выполнению |

## Схема квартиры: цвет стен и акценты (б/м)

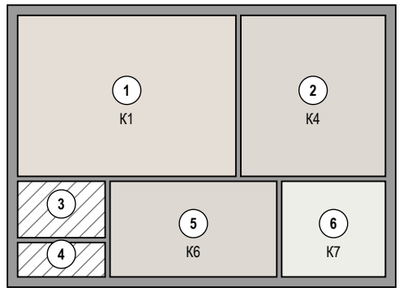


## Схема палитры проекта

Стиль: Скандинавский · схема: нейтральная

| основной | основной | основной | второстепенный | акцентный |
|---|---|---|---|---|
| **NCS S 1502-Y50R** | **NCS S 1002-Y50R** | **NCS S 0300-N** | **Tikkurila V503** | **NCS S 4010-R90B** |
| тёплый светло-серый<br>LRV 72<br>стены 2,5 | тёплый светлый грейж<br>LRV 82<br>стены 1 | белый<br>LRV 92<br>потолок 1,2,3,4,5; плинтус 1,2,5 | Winter<br>LRV 86<br>стены 6; потолок 6; плинтус 6 | пыльный синий<br>LRV 27<br>в отделке не применён |

План 60/30/10

| 60% | 30% | 10% |
|---|---|---|

Окраска, факт — по площади стен, акцентов, потолков

| 83% | 17% |
|---|---|

окрашено всего 177,7 м²; второстепенный тон несут мебель и текстиль

## Условные обозначения

- **К1** NCS S 1002-Y50R · Tikkurila · полуматов. · кл. 1
- **К2** NCS S 0300-N · Tikkurila · глубокомат. · кл. 1
- **К3** NCS S 0300-N · Orac Decor Luxxus · полуматов.
- **К4** NCS S 1502-Y50R · Tikkurila · глубокомат. · кл. 2
- **К5** NCS S 0300-N · Tikkurila · глубокомат. · кл. 2
- **К6** NCS S 1502-Y50R · Tikkurila · полуматов. · кл. 1
- **К7** Tikkurila V503 · Winter · Harmony · матовая · кл. 1
- **К8** Tikkurila V503 · Winter · Anti-Reflex 2 · глубокомат. · кл. 2
- **К9** Tikkurila V503 · Winter · Luxxus
- **КМ1** аналог: инженерная доска, дуб натуральный, масло, 1-полосная, 14/4 мм
- **КМ2** плитка · 610015000370
- **КМ3** керамогранит · SG651622R

дерево (доска, паркет, ламинат) — рисунок досок

керамогранит, плитка, камень — сетка швов по формату

плашка не залита — цвет только по коду и вееру бренда

К — краска, КМ — отделочный материал (тон КМ — по описанию, эталон — образец материала); кл. — класс истирания (1 — самый стойкий к мытью); LRV — светлота цвета: 0 — чёрный, 100 — белый

## Примечания

1. Цвет на листе и на экране — ориентир. До покраски — выкрас на объекте: не меньше А3 (или лист ГКЛ), на грунте под эту краску, не на белой шпаклёвке, в 2 слоя; на обороте — код, бренд, веер, дата. Смотреть днём и вечером, рядом с образцами пола и плитки; к основному цвету стен — ещё 2 соседних оттенка. Красить только в цвет утверждённого выкраса.
2. Краску заказывать по коду из графы «Система и код цвета» у бренда этого кода, не «аналогом» другого; весь объём одного кода — одной партией, колеруемую краску — за один проход машины.
3. Площади — те же, что в ведомости отделки (лист 48); сколько краски заказать — в спецификации отделочных материалов (лист 50).

**Допущения и предложения на листе**

Основа листа: размеры сняты с плана заказчика, контрольный обмер не выполнен (К-5); высота потолка 2700 мм принята: на плане заказчика не указана (К-5); подрайон климата не задан — принят не северный (жилые от 2,5 м) (К-4); толщины стен приняты: наружные 250 мм, перегородки 120 мм — не обмерены (К-5); разрешённая мощность 15 кВт принята по типовой квартире, технических условий нет (К-6).

Знак «**» — предложение проектировщика, заказчиком не утверждено (согласовать с заказчиком): пол пом. 1, 2, 6 — артикул изделия не выбран: позиция описана характеристиками («аналог по характеристикам»), артикул выбирается при закупке.

См. лист открытых вопросов (лист 6, записи К-4–К-6).

| Изм. | Кол.уч | Лист | № док. | Подп. | Дата |
|---|---|---|---|---|---|
| Разраб. | | Кырлан А.С. | | | 04.11.26 |
| Пров. | | | | | |
| ГИП | | | | | |
| | | | | | |
| Н. контр. | | | | | |
| Утв. | | | | | |

**ГД-2026-006-АИ**

Квартира 58 м²

Общая площадь 55,23* м² · * размеры приняты, не замерены (реестр — л. 6, 7, К-5)

Дизайн-проект интерьера

| Стадия | Лист | Листов |
|---|---|---|
| РП | 49 | 87 |

**Колерная карта**

М б/м

**Кырлан Александр Сергеевич**

# Спецификация отделочных материалов

Форма 1 по ГОСТ 21.110-2013 · количества — из геометрии проекта, с запасом

**ПРЕДВАРИТЕЛЬНО · не для производства работ · открыто пунктов: 10 (реестр — л. 6, 7)**

| Поз. | Наименование и техническая характеристика | Тип, марка, обозначение документа | Код продукции | Поставщик | Ед. изм. | Кол. | Масса 1 ед., кг | Примечание |
|---|---|---|---|---|---|---|---|---|
| | **Лакокрасочные материалы** | | | | | | | |
| 1 | Краска интерьерная водно-дисперсионная акриловая для стен, полуматовая, класс мокрого истирания 1 по EN 13300, база A; цвет NCS S 1002-Y50R, колеровка машинная | Tikkurila | | Tikkurila | л | 11,7 | | поз. К1 колерной карты; пом. 1; S = 41,2 м² × 2 сл. × 0,12 л/м² = 9,9 л, +10 % и 0,5 л на подкраску → ≥ 11,4 л; тара 1 × 9 л + 1 × 2,7 л |
| 2 | Краска интерьерная водно-дисперсионная для потолков, глубокоматовая, класс мокрого истирания 1 по EN 13300, база A; цвет NCS S 0300-N, колеровка машинная | Tikkurila | | Tikkurila | л | 9,9 | | поз. К2 колерной карты; пом. 1, 3, 4, 5; S = 35,3 м² × 2 сл. × 0,12 л/м² = 8,5 л, +10 % и 0,5 л на подкраску → ≥ 9,8 л; тара 1 × 9 л + 1 × 0,9 л |
| 3 | Краска интерьерная водно-дисперсионная акриловая для стен, глубокоматовая, класс мокрого истирания 2 по EN 13300, база A; цвет NCS S 1502-Y50R, колеровка машинная | Tikkurila | | Tikkurila | л | 9,9 | | поз. К4 колерной карты; пом. 2; S = 33,9 м² × 2 сл. × 0,12 л/м² = 8,1 л, +10 % и 0,5 л на подкраску → ≥ 9,5 л; тара 1 × 9 л + 1 × 0,9 л |
| 4 | Краска интерьерная водно-дисперсионная для потолков, глубокоматовая, класс мокрого истирания 2 по EN 13300, база A; цвет NCS S 0300-N, колеровка машинная | Tikkurila | | Tikkurila | л | 4,5 | | поз. К5 колерной карты; пом. 2; S = 13,9 м² × 2 сл. × 0,12 л/м² = 3,3 л, +10 % и 0,5 л на подкраску → ≥ 4,2 л; тара 1 × 2,7 л + 2 × 0,9 л |
| 5 | Краска интерьерная водно-дисперсионная акриловая для стен, полуматовая, класс мокрого истирания 1 по EN 13300, база A; цвет NCS S 1502-Y50R, колеровка машинная | Tikkurila | | Tikkurila | л | 7,2 | | поз. К6 колерной карты; пом. 5; S = 22,7 м² × 2 сл. × 0,12 л/м² = 5,4 л, +10 % и 0,5 л на подкраску → ≥ 6,5 л; тара 2 × 2,7 л + 2 × 0,9 л |
| 6 | Краска интерьерная водно-дисперсионная акриловая для стен, матовая, класс мокрого истирания 1 по EN 13300, база A; цвет по вееру Tikkurila V503 «Winter», колеровка машинная | Tikkurila Harmony | | Tikkurila | л | 7,2 | | поз. К7 колерной карты; пом. 6; S = 24,7 м² × 2 сл. × 0,12 л/м² = 5,9 л, +10 % и 0,5 л на подкраску → ≥ 7,0 л; тара 2 × 2,7 л + 2 × 0,9 л |
| 7 | Краска интерьерная водно-дисперсионная акриловая для потолков, глубокоматовая, класс мокрого истирания 2 по EN 13300, база A; цвет по вееру Tikkurila V503 «Winter», колеровка машинная | Tikkurila Anti-Reflex 2 | | Tikkurila | л | 2,7 | | поз. К8 колерной карты; пом. 6; S = 5,9 м² × 2 сл. × 0,12 л/м² = 1,4 л, +10 % и 0,5 л на подкраску → ≥ 2,1 л; тара 1 × 2,7 л |
| 8 | Акрил, полуматовая в цвет NCS S 0300-N — окраска плинтуса | аналог по характеристикам | | | л | 1,4 | | поз. К3; пом. 1, 2, 5; L = 39,9 м, S = 5,0 м² × 2 сл. × 0,12 л/м² + 10 %; продукт подобрать в веере NCS |
| 9 | Краска для МДФ и дерева в цвет Tikkurila V503 «Winter» — окраска плинтуса; блеск не ниже блеска стен | марка не задана | | | л | 0,5 | | поз. К9; пом. 6; L = 9,0 м, S = 1,1 м² × 2 сл. × 0,12 л/м² + 10 %; продукт подобрать в веере Tikkurila |
| 10 | Грунтовка акриловая под окраску стен и потолков — из системы производителя краски | по системе краски | | | м² | 178 | | площадь окраски стен, акцентов и потолков; 1 слой перед окраской; расход — по ТУ грунтовки |
| | **Плитка и керамогранит** | | | | | | | |
| 11 | SG651622R, 600×600 мм, противоскольжение R10 | SG651622R | | Kerama Marazzi | м² | 19,44 | | шов 2 мм; Ванная, пол; Санузел, пол; Прихожая, пол; по раскладке 48 шт (S = 14,30 м²), с запасом 54 шт |
| 12 | 610015000370, 1200×600 мм | 610015000370 | | Italon | м² | 70,56 | | шов 2 мм; Ванная, стены А–Г; Ванная, короб стояков Ш1 489×319; Санузел, стены А–Г; Санузел, короб инсталляции; по раскладке 87 шт (S = 31,81 м²), с запасом 98 шт |
| | **Напольные покрытия** | | | | | | | |
| 13 | Инженерная доска, дуб натуральный, масло, 1-полосная, 14/4 мм, класс 33, эмиссия E1, укладка на клей | аналог по характеристикам | | | м² | 37,5 | | пом. 1, 2; S = 34,99 м² + 7 % (прямая укладка); к заказу — кратно упаковке |
| 14 | Инженерная доска, дуб натуральный, масло, 1-полосная, 14/4 мм, эмиссия E1, укладка на клей | аналог по характеристикам | | | м² | 6,4 | | пом. 6; S = 5,94 м² + 7 % (прямая укладка); к заказу — кратно упаковке |
| 15 | Клей для паркета и инженерной доски, эластичный (СМП / полиуретановый) | по рекомендации производителя доски | | | м² | 41 | | площадь приклейки; расход и шпатель — по ТУ клея |
| | **Погонажные изделия** | | | | | | | |
| 16 | SX184, h = 110 мм, крепление к стене, окраска в цвет NCS S 0300-N | SX184 | | Orac Decor | м | 44 | | пом. 1, 2, 5; L = 39,9 м (периметр без дверных проёмов) + 10 % на подрезку; в штуках — по длине планки |
| 17 | SX184, h = 110 мм, крепление к стене, окраска в цвет Tikkurila V503 | SX184 | | Orac Decor | м | 10 | | пом. 6; L = 9,0 м (периметр без дверных проёмов) + 10 % на подрезку; в штуках — по длине планки |
| | **Смеси и материалы для облицовки** | | | | | | | |
| 18 | Затирка для швов плитки | аналог по характеристикам | | | кг | 3,9 | | по раскладке (a+b)/(a·b) × шов × t × 1,6 + 10 % |
| 19 | Клей плиточный C2 S1 по EN 12004, слой 5 мм | аналог по характеристикам | | | кг | 35 | | 2 меш. по 25 кг; 1,5 кг/м² на 1 мм слоя + 10 % |
| 20 | Клей плиточный C2 по EN 12004, слой 5 мм | аналог по характеристикам | | | кг | 332 | | 14 меш. по 25 кг; 1,5 кг/м² на 1 мм слоя + 10 % |
| 21 | Гидроизоляция обмазочная мокрых зон: пол, стены по периметру, зоны замачивания; 2 слоя с армирующей лентой в углах | аналог по характеристикам | | | м² | 13,4 | | площадь по листу раскладки плитки + 10 %; расход смеси — по ТУ |
| 22 | Лента демпферная по периметру пола из плитки | аналог по характеристикам | | | м | 21 | | периметр без дверных проёмов + 10 % |

## Примечания

1. Количества — из геометрии проекта: площади поверхностей по чистым граням стен до отделки (те же, что в ведомости отделки и колерной карте), плитка, клей и затирка — по раскладке плиточника; в графе «Кол.» — к заказу, с запасом.
2. Краска: расход 0,12 л/м² на слой в 2 слоя, если по ТУ не задан иной; запас 10 % и 0,5 л на подкраску каждого кода. Один код — одна партия, колеровка машинная в колеровочном центре бренда; в заказ — только после утверждения выкраса (колерная карта). Фасовка — по каталогу бренда на дату выпуска; к заказу — не меньше расчётного объёма.
3. «Аналог по характеристикам» — допускается изделие другого производителя с характеристиками не ниже указанных, по согласованию с автором проекта.
4. Графы «Код продукции» и «Масса 1 ед.» не заполнены: коды по классификатору продукции не присвоены, масса единицы до 25 кг (ГОСТ 21.110-2013).
5. Грунтовка и клей для доски указаны площадью обработки; объём — по ТУ выбранного продукта.

**Допущения и предложения на листе**

Основа листа: размеры сняты с плана заказчика, контрольный обмер не выполнен (К-5); высота потолка 2700 мм принята: на плане заказчика не указана (К-5); подрайон климата не задан — принят не северный (жилые от 2,5 м) (К-4); толщины стен приняты: наружные 250 мм, перегородки 120 мм — не обмерены (К-5); разрешённая мощность 15 кВт принята по типовой квартире, технических условий нет (К-6).

Знак «**» — предложение проектировщика, заказчиком не утверждено (согласовать с заказчиком): пол пом. 1, 2, 6 — артикул изделия не выбран: позиция описана характеристиками («аналог по характеристикам»), артикул выбирается при закупке.

См. лист открытых вопросов (лист 6, записи К-4–К-6).

| Изм. | Кол.уч | Лист | № док. | Подп. | Дата |
|---|---|---|---|---|---|
| Разраб. | | Кырлан А.С. | | | 04.11.26 |
| Пров. | | | | | |
| ГИП | | | | | |
| | | | | | |
| Н. контр. | | | | | |
| Утв. | | | | | |

**ГД-2026-006-АИ**

Квартира 58 м²

Общая площадь 55,23* м² · * размеры приняты, не замерены (реестр — л. 6, 7, К-5)

Дизайн-проект интерьера

| Стадия | Лист | Листов |
|---|---|---|
| РП | 50 | 87 |

**Спецификация отделочных материалов**

М б/м

**Кырлан Александр Сергеевич**

# Концепция декора и визуализации


Скандинавский · кухня-гостиная и спальня · визуализации, палитра, материалы, ключевые предметы

**ПРЕДВАРИТЕЛЬНО · не для производства работ · открыто пунктов: 10 (реестр — л. 6, 7)**

место под визуализацию: вид сверху (3D) с мебелью, текстилем и декором

**Вид сверху (3D) — визуализация в работе**

Расстановка — по плану мебели (лист 18); шторы, ковры, картины и растения — по плану текстиля и декора.

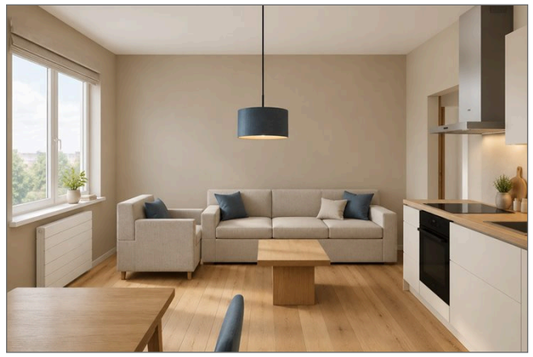

**Визуализация 7. Кухня-гостиная (пом. 1)**



**Визуализация 3. Спальня (пом. 2)**



**Визуализация 1. Ванная (пом. 3)**



**Визуализация 11. Санузел (пом. 4)**

## Материалы и фактуры



**Дуб натуральный**

пол: пом. 1, 2, 6

**Допущения и предложения на листе**

Основа листа: размеры сняты с плана заказчика, контрольный обмер не выполнен (К-5); высота потолка 2700 мм принята: на плане заказчика не указана (К-5); подрайон климата не задан — принят не северный (жилые от 2,5 м) (К-4); толщины стен приняты: наружные 250 мм, перегородки 120 мм — не обмерены (К-5); разрешённая мощность 15 кВт принята по типовой квартире, технических условий нет (К-6).

Знак «**» — предложение проектировщика, заказчиком не утверждено (согласовать с заказчиком): ИЗ-2: М1 — Было offset 1300…3500: торец дивана в 500 мм от стены В, правые 350 мм проёма Д-2 (3900…4800) упирались в диван.

См. лист открытых вопросов (лист 6, записи К-4–К-6; лист 7, запись ИЗ-2).

## Ключевые предметы

— Диван М1** 2200×950 — кухня-гостиная

— Кровати С1

## Палитра 60/30/10 и цвета текстиля




- NCS S 1502-Y50R (тёплый светло-серый), LRV 72 — 60 % база
- NCS S 1002-Y50R (тёплый светлый грейж), LRV 82 — 60 % база
- Tikkurila V503 (Winter), LRV 86 — 30 % второй цвет
- NCS S 4010-R90B (пыльный синий), LRV 27 — 10 % акцент

## Настроение

Палитра выведена из выкрасов (колерная карта): база — тёплые нейтрали NCS S 1502-Y50R / S 1002-Y50R на стенах, NCS S 0300-N на потолках; второй цвет — Tikkurila V503 (гардеробная); акцент — пыльный синий NCS S 4010-R90B в текстиле по концепции стиля (текстиль в данных ещё не задан). Настроение стиля: светло, спокойно, уютно (hygge), естественно, функционально, в меру (lagom). Свет тёплый, 2700–3000 K.

## Примечания

1. Визуализации — образ интерьера. Изделия, размеры, высоты подвеса и привязки — по чертежам; при расхождении действуют чертежи и ведомости.
2. Коды цвета — ориентир подбора по веерам производителей; ткань утверждается по образцу при дневном свете и при свете проекта 2700–3000 K.
3. Мелкий стайлинг на визуализациях (книги, посуда, свечи) в ведомости не входит и поставляется заказчиком по желанию.


| | | | | | | | | |
|---|---|---|---|---|---|---|---|---|
| | | | | | | **ГД-2026-006-АИ** | | |
| | | | | | | Квартира 58 м² | | |
| | | | | | | Общая площадь 55,23* м² · * размеры приняты, не замерены (реестр — л. 6, 7, К-5) | | |
| Изм. | Кол.уч | Лист | № док. | Подп. | Дата | Дизайн-проект интерьера | Стадия | Лист | Листов |
| Разраб. | | Кырлан А.С. | | | 04.11.26 | | РП | 51 | 87 |
| Пров. | | | | | | | | | |
| ГИП | | | | | | | | | |
| | | | | | | **Концепция декора и визуализации** | **Кырлан Александр Сергеевич** | | |
| Н. контр. | | | | | | М б/м | | | |
| Утв. | | | | | | | | | |

выпуск 04.11.2026 № 3da8f16a26 · стр. 58 из 96

# Встроенная мебель. Схема расположения

встроенная и корпусная мебель на заказ, кухонный гарнитур · размеры в мм · марки — по ведомости изделий

**ПРЕДВАРИТЕЛЬНО · не для производства работ · открыто пунктов: 10 (реестр — л. 6, 7)**

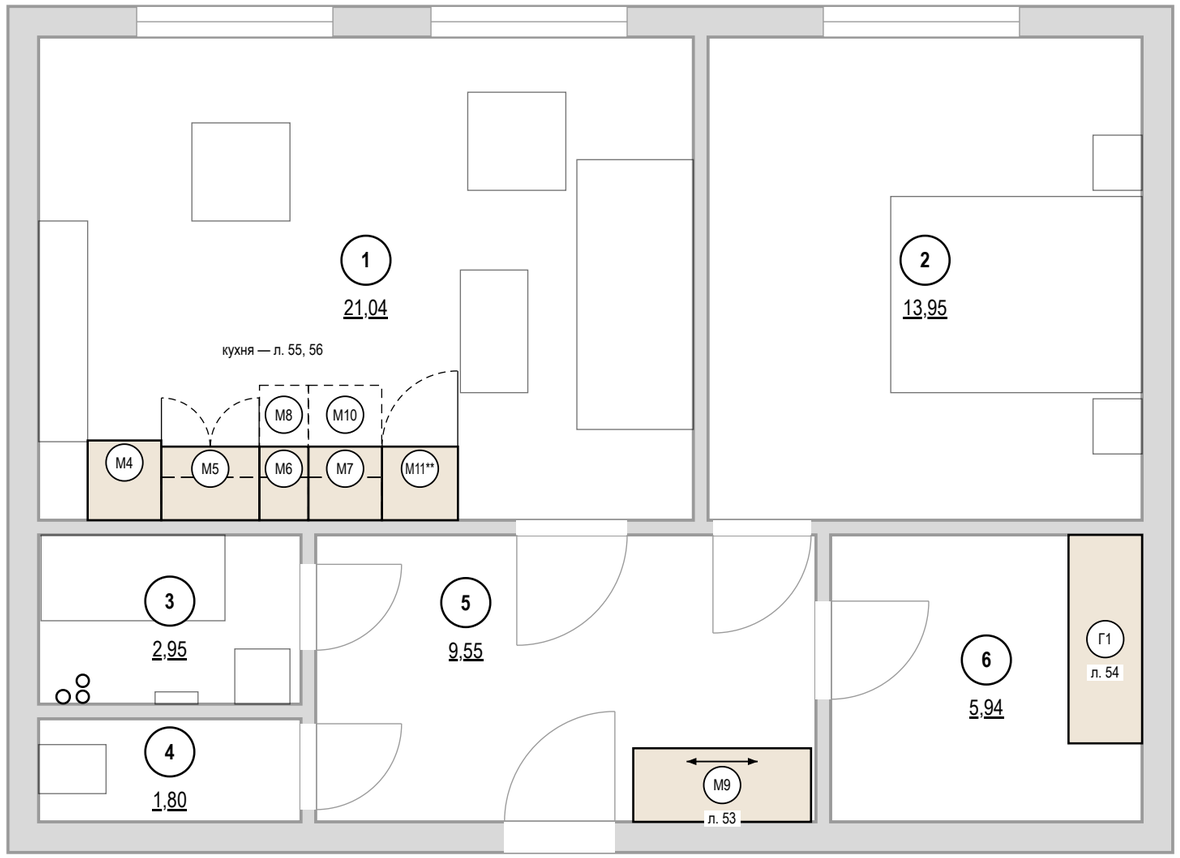


## Ведомость изделий

| Марка | Наименование | Пом. | Ш×Г×В, мм | Лист |
|---|---|---|---|---|
| М9 | Шкаф-купе | 5 | 1450×600×2450 | 53 |
| Г1 | Система хранения | 6 | 1700×600×2400 | 54 |
| М11** | Ниша под стиральную машину 620: без корпуса, между боковинами соседних модулей, фасад на петлях к боковине соседнего модуля; цоколь съёмный | 1 | 620×600×900 | 55 |
| М7 | Модуль нижний: ящики, варочная | 1 | 600×600×900 | 55 |
| М10 | Модуль навесной: полки | 1 | 600×350×620 | 55 |
| М6 | Модуль нижний: ящики | 1 | 400×600×900 | 55 |
| М8 | Модуль навесной: полки, сушка | 1 | 1200×350×720 | 55 |
| М5 | Модуль нижний: мойка | 1 | 800×600×900 | 55 |
| М4 | Место под холодильник отдельностоящий: без корпуса и фасада | 1 | 600×650×2100 | 55 |

## Условные обозначения

- изделие мебельщика: корпус на полу
- невидимый контур: навесной модуль, корпус под столешницей
- открывание распашного фасада
- зона выдвижения ящика, двери техники
- дверь купе, стрелка — направление движения
- К1 — марка изделия или модуля (на схеме расположения под ней — лист изделия)

**Допущения и предложения на листе**

Основа листа: размеры сняты с плана заказчика, контрольный обмер не выполнен (К-5); высота потолка 2700 мм принята: на плане заказчика не указана (К-5); подрайон климата не задан — принят не северный (жилые от 2,5 м) (К-4); толщины стен приняты: наружные 250 мм, перегородки 120 мм — не обмерены (К-5); разрешённая мощность 15 кВт принята по типовой квартире, технических условий нет (К-6).

Знак «**» — предложение проектировщика, заказчиком не утверждено (согласовать с заказчиком): К-7: М11 — место стиральной машины: вместо модуля с ящиками 400 справа от варочной; ряд до 3420, журнальный стол М21 (с х 3440) не мешает загрузке.

См. лист открытых вопросов (лист 6, записи К-4–К-7).

## Примечания

1. Изделия — по чистовым размерам помещений; перед раскроем — контрольный замер цеха после чистовой отделки стен, пола и потолка.
2. Открывание фасадов и выдвижение ящиков показано в открытом положении: зоны не пересекают двери, радиаторы, выключатели и проходы.
3. Стояки и счётчики за мебелью — с сервисным люком; газовые трубы мебелью не зашиваются.
4. Покупная мебель — по плану расстановки мебели и спецификации дизайнера; здесь — подложкой.

1000 мм · печать 1:1

| Изм. | Кол.уч | Лист | № док. | Подп. | Дата |
|---|---|---|---|---|---|
| Разраб. | | Кырлан А.С. | | | 04.11.26 |
| Пров. | | | | | |
| ГИП | | | | | |
| | | | | | |
| Н. контр. | | | | | |
| Утв. | | | | | |

**ГД-2026-006-АИ**

Квартира 58 м²

Общая площадь 55,23* м² · * размеры приняты, не замерены (реестр — л. 6, 7, К-5)

Дизайн-проект интерьера

| Стадия | Лист | Листов |
|---|---|---|
| РП | 52 | 87 |

**Встроенная мебель. Схема расположения**

М 1:50

**Кырлан Александр Сергеевич**


выпуск 04.11.2026 № 3da8f16a26 · стр. 59 из 96

# Шкаф-купе М9


Прихожая (пом. 5) · вид из помещения · размеры в мм, отметки в м

ПРЕДВАРИТЕЛЬНО · не для производства работ · открыто пунктов: 10 (реестр — л. 6, 7)


**Вид с фасадами**

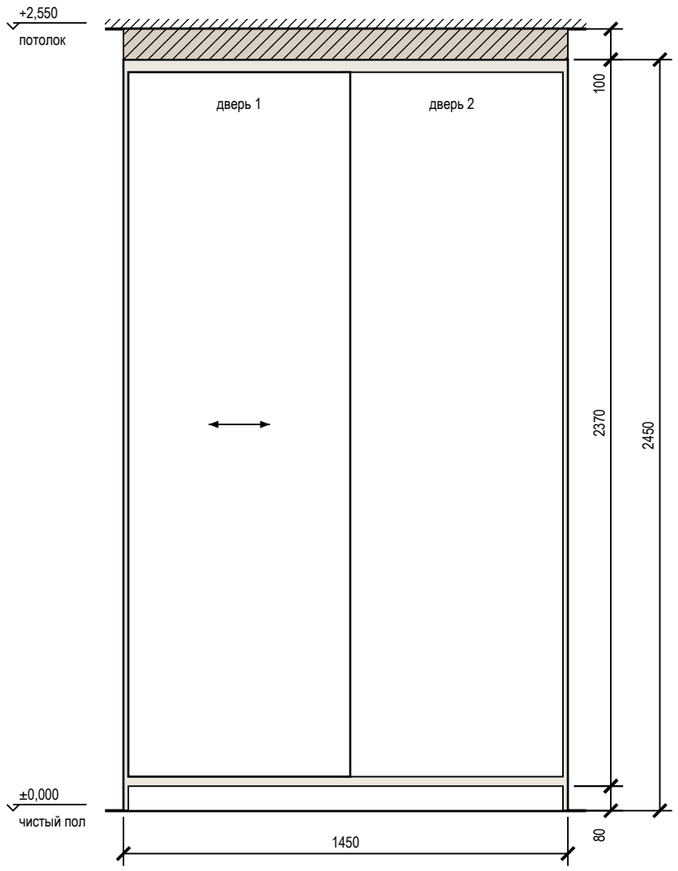



**Вид без фасадов**

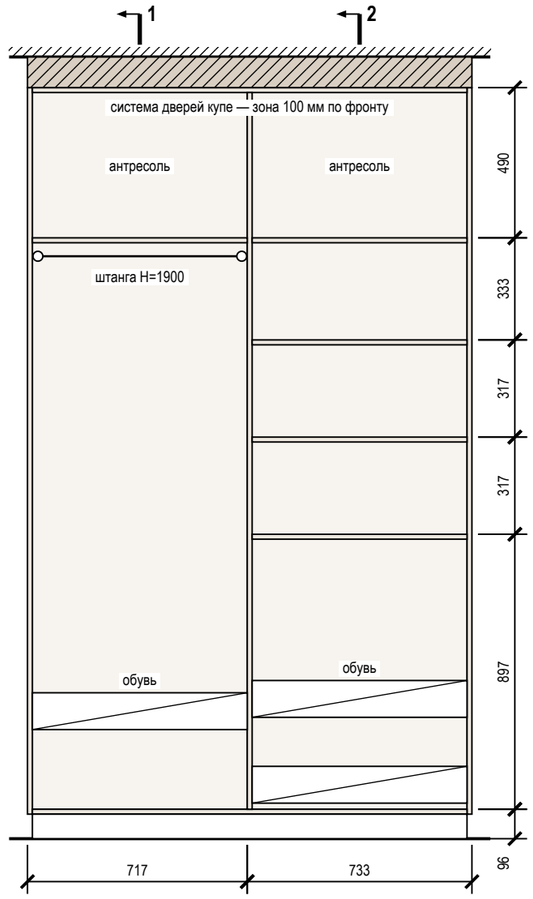


**Разрез 1-1**

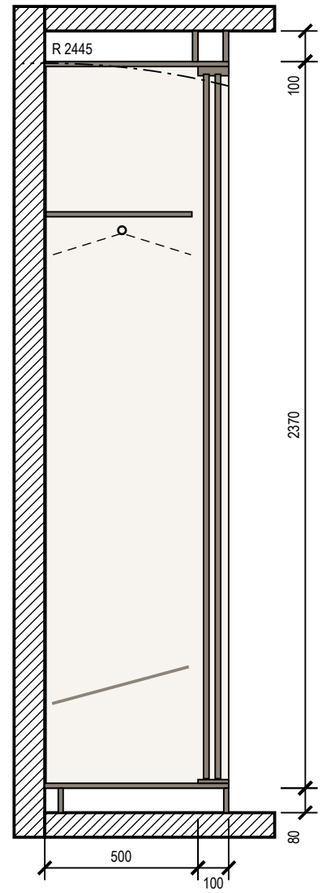


**Разрез 2-2**

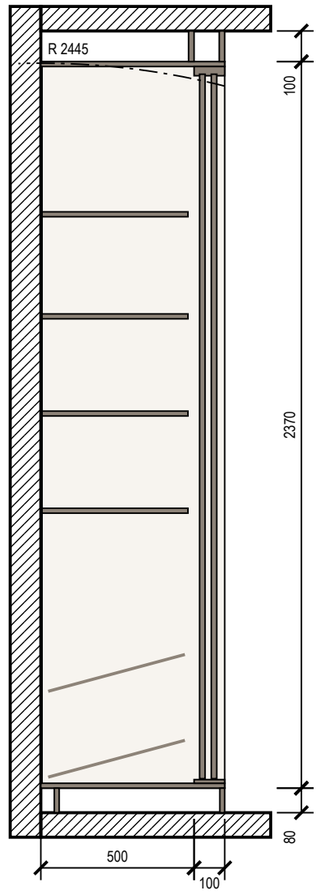


## Примечания

1. Размеры — в мм по чистовой отделке; изделие 1450×600×2450 (Ш×Г×В). Перед раскроем — контрольный замер цеха после чистовой отделки стен, пола и потолка.
2. Корпус — ЛДСП 16 мм, задняя стенка ХДФ 4 мм в паз, цоколь 80 мм на регулируемых опорах; двери купе — ЛДСП 10 мм в алюминиевом профиле; нахлёст 30 мм, ширина двери 724 мм, высота — проём минус 40 мм; цвет — по колерной карте.
3. Кромка: скрытые торцы 0,4 мм, видимые 1 мм (ПВХ/АБС).
4. Номинальные зазоры: дверь купе — боковина 3 мм, фасад ящика — стойка 2 мм; ящики внутри купе — с накладкой 30 мм на стойке со стороны нахлёста дверей.
5. Присадка по 32-й системе — выполняет цех.
6. Компенсатор 100 мм — короб из ЛДСП по фронту и торцам, подгоняется к потолку при монтаже (припуск 20 мм), крепится к корпусу и к потолку.
7. Подъём корпуса: диагональ боковины без цоколя √(2370² + 600²) = 2445 мм < 2550 мм до потолка — корпус собирается лёжа, поднимается поворотом и ставится на цоколь.
8. Крепление к стене от опрокидывания — уголки 2 шт. к несущему основанию (монтажная схема шкафов).

## Условные обозначения

- дверь купе, стрелка — направление движения
- корпус и полки ЛДСП (вид на стену)
- задняя стенка ХДФ
- деталь в разрезе
- компенсатор — короб до потолка
- штанга для плечиков (на разрезе — плечики 450 мм)
- траектория угла корпуса при подъёме в проектное положение

**Допущения и предложения на листе**

Основа листа: размеры сняты с плана заказчика, контрольный обмер не выполнен (К-5); высота потолка 2700 мм принята: на плане заказчика не указана (К-5); подрайон климата не задан — принят не северный (жилые от 2,5 м) (К-4); толщины стен приняты: наружные 250 мм, перегородки 120 мм — не обмерены (К-5); разрешённая мощность 15 кВт принята по типовой квартире, технических условий нет (К-6).

См. лист открытых вопросов (лист 6, записи К-4–К-6).

1000 мм · печать 1:1

| Изм. | Кол.уч | Лист | № док. | Подп. | Дата |
|---|---|---|---|---|---|
| Разраб. | | Кырлан А.С. | | | 04.11.26 |
| Пров. | | | | | |
| ГИП | | | | | |
| | | | | | |
| Н. контр. | | | | | |
| Утв. | | | | | |

**ГД-2026-006-АИ**

Квартира 58 м²

Общая площадь 55,23* м² · * размеры приняты, не замерены (реестр — л. 6, 7, К-5)

Дизайн-проект интерьера

| Стадия | Лист | Листов |
|---|---|---|
| РП | 53 | 87 |

**Шкаф-купе М9**

М 1:20

Кырлан Александр Сергеевич


выпуск 04.11.2026 № 3da8f16a26 · стр. 60 из 96

# Система хранения Г1


Гардеробная (пом. 6) · вид из помещения · размеры в мм, отметки в м

ПРЕДВАРИТЕЛЬНО · не для производства работ · открыто пунктов: 10 (реестр — л. 6, 7)


**Общий вид**

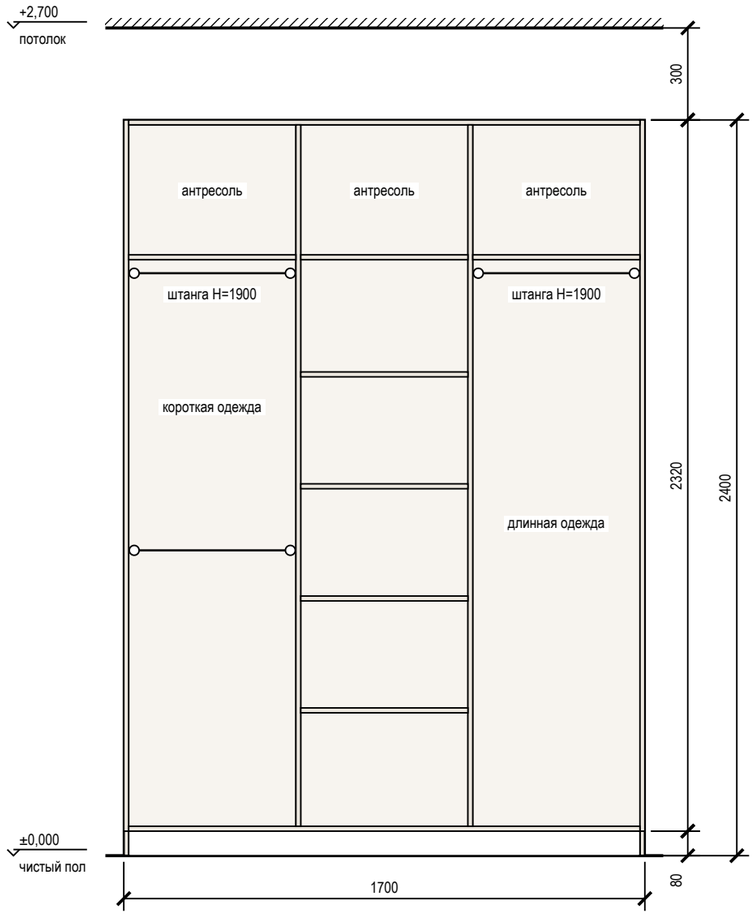



**Наполнение, размеры в свету**

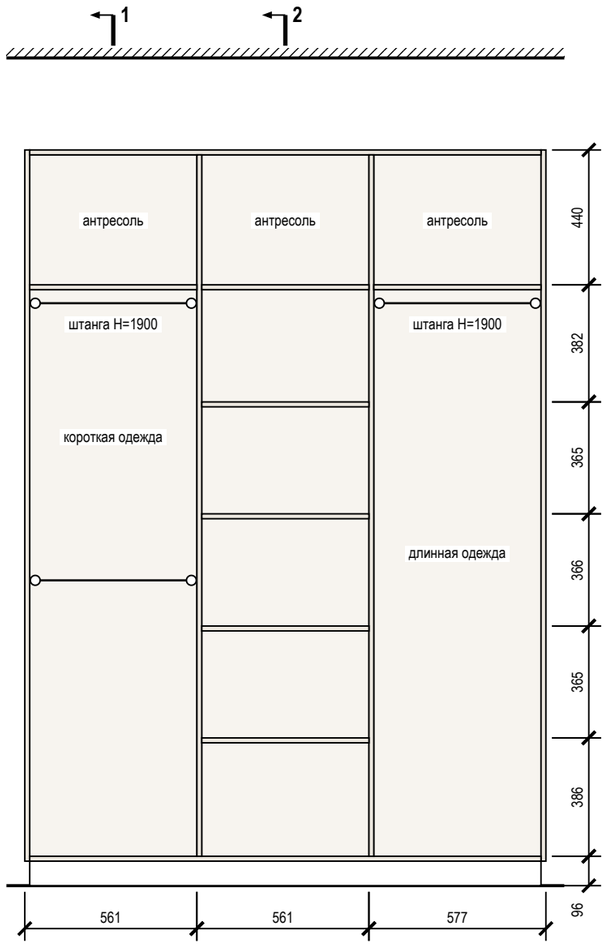


**Разрез 1-1**

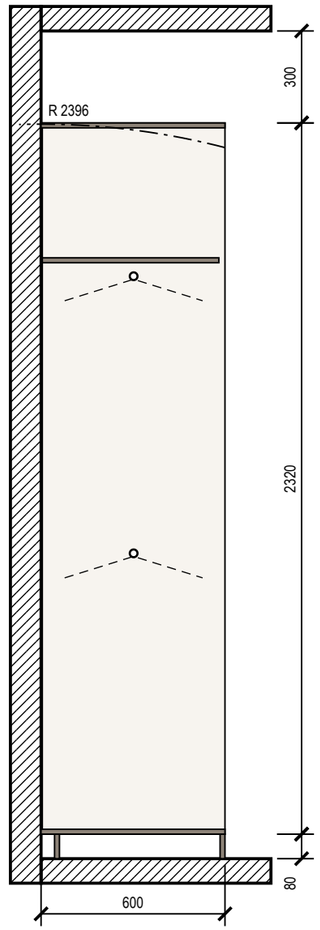


**Разрез 2-2**

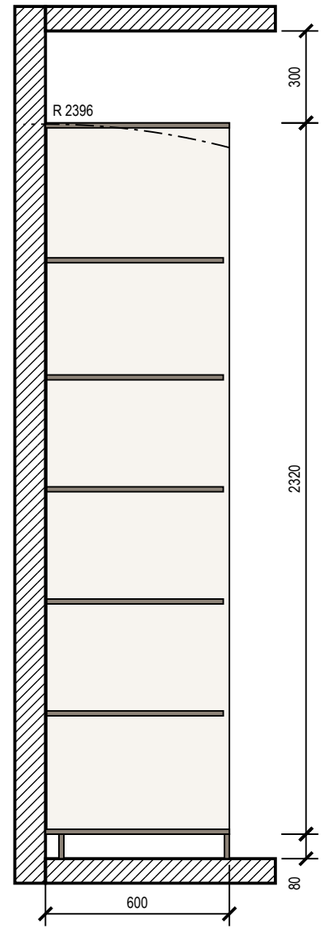


## Примечания

1. Размеры — в мм по чистовой отделке; изделие 1700×600×2400 (Ш×Г×В). Перед раскроем — контрольный замер цеха после чистовой отделки стен, пола и потолка.
2. Корпус — ЛДСП 16 мм, задняя стенка ХДФ 4 мм в паз, цоколь 80 мм на регулируемых опорах; открытая система: без фасадов.
3. Кромка: скрытые торцы 0,4 мм, видимые 2 мм (ПВХ/АБС).
4. Присадка по 32-й системе — выполняет цех.
5. Зазор до потолка 300 мм.
6. Подъём корпуса: диагональ боковины без цоколя √(2320² + 600²) = 2396 мм < 2700 мм до потолка — корпус собирается лёжа, поднимается поворотом и ставится на цоколь.
7. Крепление к стене от опрокидывания: крепление к стене, 3 точки; основание стены и шаг анкеров — монтажная схема шкафов.

## Условные обозначения

- корпус и полки ЛДСП (вид на стену)
- задняя стенка ХДФ
- деталь в разрезе
- штанга для плечиков (на разрезе — плечики 450 мм)
- траектория угла корпуса при подъёме в проектное положение

**Допущения и предложения на листе**

Основа листа: размеры сняты с плана заказчика, контрольный обмер не выполнен (К-5); высота потолка 2700 мм принята: на плане заказчика не указана (К-5); подрайон климата не задан — принят не северный (жилые от 2,5 м) (К-4); толщины стен приняты: наружные 250 мм, перегородки 120 мм — не обмерены (К-5); разрешённая мощность 15 кВт принята по типовой квартире, технических условий нет (К-6).

См. лист открытых вопросов (лист 6, записи К-4–К-6).

1000 мм · печать 1:1

| Изм. | Кол.уч | Лист | № док. | Подп. | Дата |
|---|---|---|---|---|---|
| Разраб. | | Кырлан А.С. | | | 04.11.26 |
| Пров. | | | | | |
| ГИП | | | | | |
| Н. контр. | | | | | |
| Утв. | | | | | |

**ГД-2026-006-АИ**

Квартира 58 м²

Общая площадь 55,23* м² · * размеры приняты, не замерены (реестр — л. 6, 7, К-5)

Дизайн-проект интерьера

| Стадия | Лист | Листов |
|---|---|---|
| РП | 54 | 87 |

**Система хранения Г1**

М 1:20

**Кырлан Александр Сергеевич**


выпуск 04.11.2026 № 3da8f16a26 · стр. 61 из 96

# Кухня (пом. 1). Развёртка гарнитура


Кухня-гостиная (пом. 1) · стена В · вид из помещения · размеры в мм, отметки в м

ПРЕДВАРИТЕЛЬНО · не для производства работ · открыто пунктов: 10 (реестр — л. 6, 7)


## Вид с фасадами

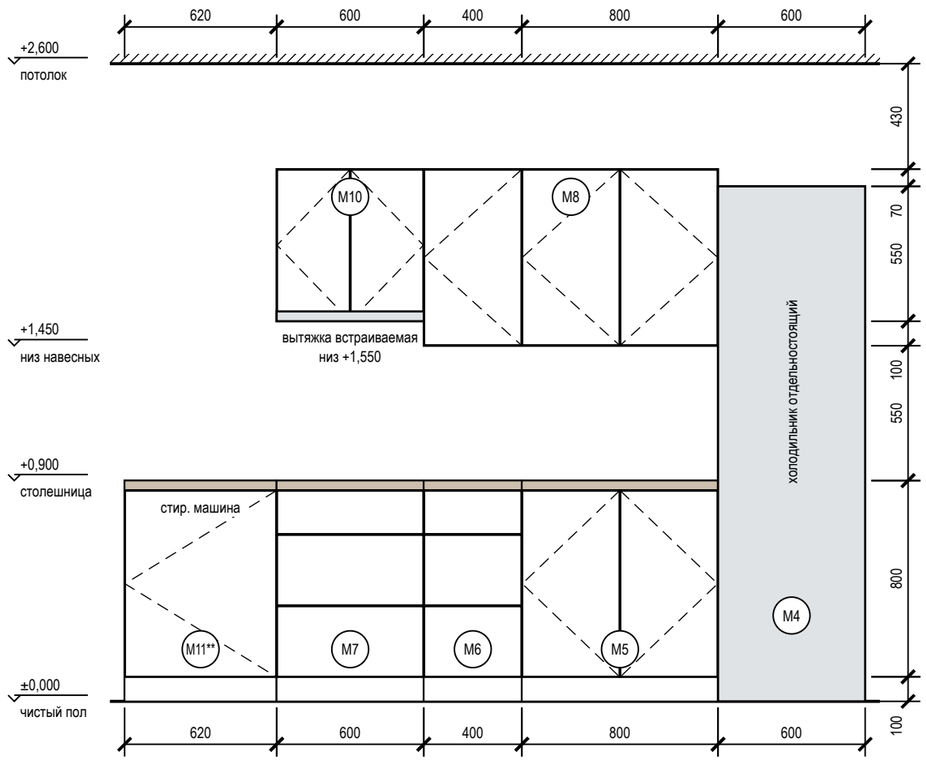



## Вид без фасадов (наполнение, выводы)

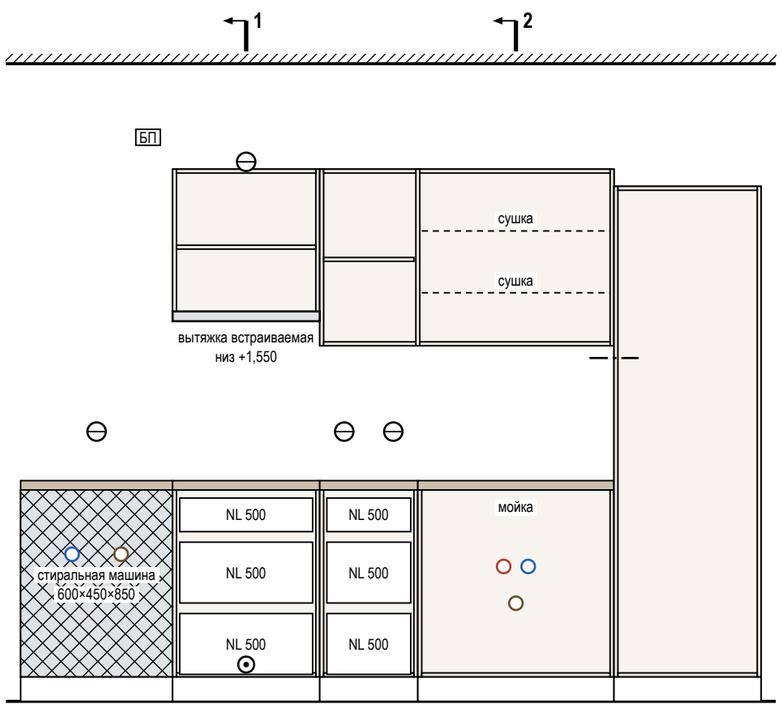


## Разрез 1-1

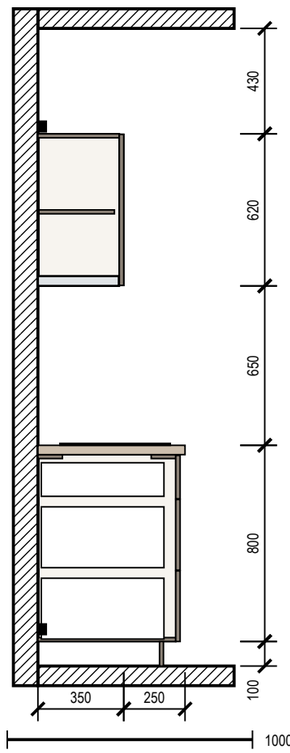


## Разрез 2-2

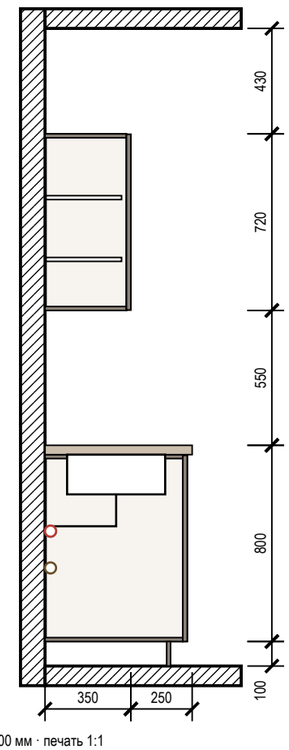


1000 мм · печать 1:1

## Условные обозначения

- фасад распашной: линии сходятся к стороне петель
- фасад ящика, карго
- встраиваемая техника
- столешница
- доборная планка
- деталь в разрезе
- К1 — марка изделия или модуля (на схеме расположения под ней — лист изделия)
- розетка на стене
- вывод кабеля к технике
- В1 — вывод воды В1 / Т3, канализации К1

## Примечания

1. Размеры — в мм по чистовой отделке, вид из помещения; марки — как на плане расстановки. Перед раскроем — контрольный замер цеха после фартука и пола.
2. Корпуса — ЛДСП 16 мм, задняя стенка ХДФ 4 мм; фасады — МДФ эмаль 18 мм, цвет по колерной карте; столешница 38 мм, свес 20 мм; цоколь 100 мм.
3. Кромка: скрытые торцы 0,4 мм, видимые 1 мм. Номинальные зазоры: между фасадами 3 мм, фасад — столешница 3 мм, фасад — стена не менее 3 мм.
4. Ящики полного выдвижения и петли — с доводчиком; присадка по 32-й системе — выполняет цех.
5. Вытяжка встраивается в дно навесного модуля М10 над варочной: её низ на 1550 мм от пола, 650 мм над панелью (не меньше 650 мм).
6. Ниши техники — по монтажным схемам выбранных моделей: решётка в цоколе и канал за пеналом холодильника, зазор за духовым шкафом, фасад ПММ на двери машины.

**Допущения и предложения на листе**

Основа листа: размеры сняты с плана заказчика, контрольный обмер не выполнен (К-5); высота потолка 2700 мм принята: на плане заказчика не указана (К-5); подрайон климата не задан — принят не северный (жилые от 2,5 м) (К-4); толщины стен приняты: наружные 250 мм, перегородки 120 мм — не обмерены (К-5); разрешённая мощность 15 кВт принята по типовой квартире, технических условий нет (К-6).

Знак «**» — предложение проектировщика, заказчиком не утверждено (согласовать с заказчиком): К-7: М11 — место стиральной машины: вместо модуля с ящиками 400 справа от варочной; ряд до 3420, журнальный стол М21 (с х 3440) не мешает загрузке.

См. лист открытых вопросов (лист 6, записи К-4–К-7).

| Изм. | Кол.уч | Лист | № док. | Подп. | Дата |
|---|---|---|---|---|---|
| Разраб. | | Кырлан А.С. | | | 04.11.26 |
| Пров. | | | | | |
| ГИП | | | | | |
| | | | | | |
| Н. контр. | | | | | |
| Утв. | | | | | |

**ГД-2026-006-АИ**

Квартира 58 м²

Общая площадь 55,23* м² · * размеры приняты, не замерены (реестр — л. 6, 7, К-5)

Дизайн-проект интерьера

| Стадия | Лист | Листов |
|---|---|---|
| РП | 55 | 87 |

**Кухня (пом. 1). Развёртка гарнитура**

М 1:25

**Кырлан Александр Сергеевич**


выпуск 04.11.2026 № 3da8f16a26 · стр. 62 из 96

# Кухня (пом. 1). Монтажная схема


Кухня-гостиная (пом. 1) · стена В · размеры в мм от чистых поверхностей, высоты — от чистого пола

ПРЕДВАРИТЕЛЬНО · не для производства работ · открыто пунктов: 10 (реестр — л. 6, 7)

## Привязка выводов и крепление модулей

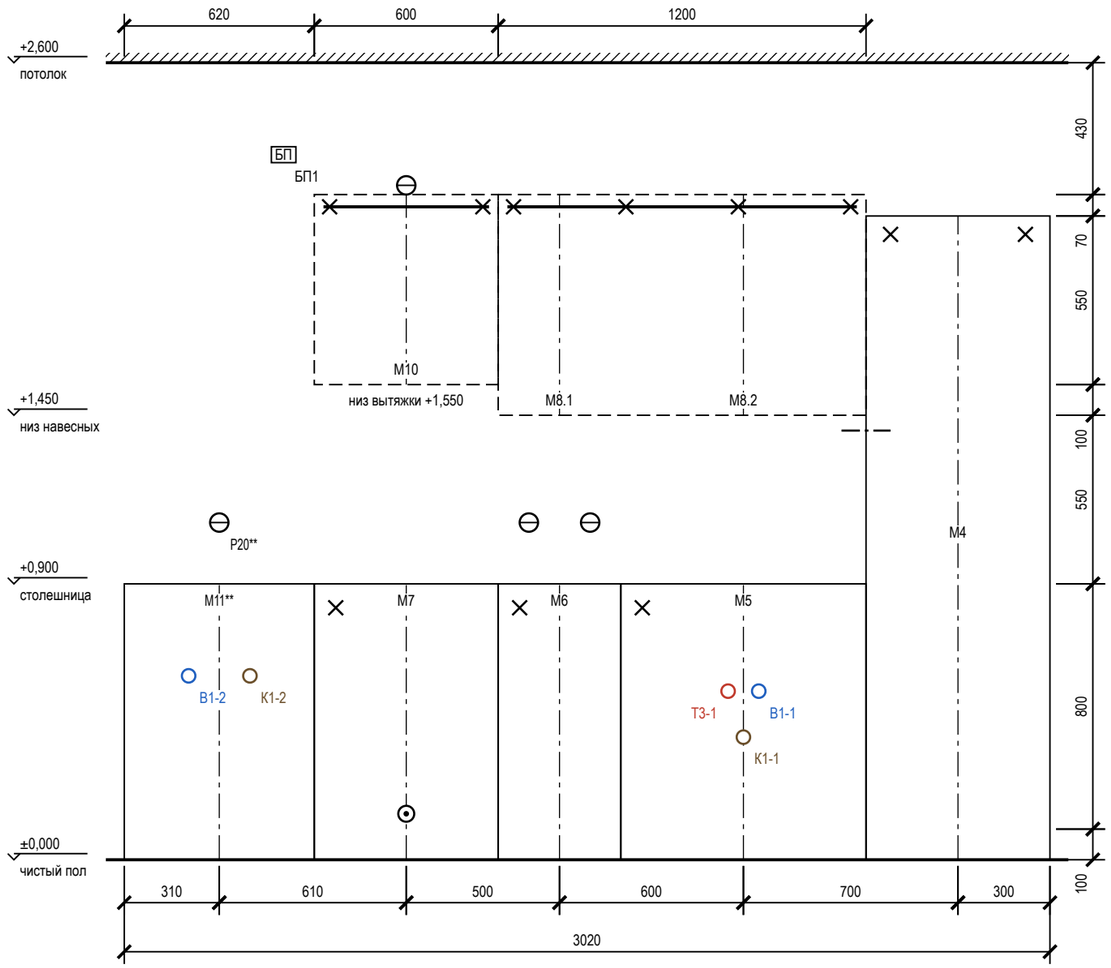


## План столешницы

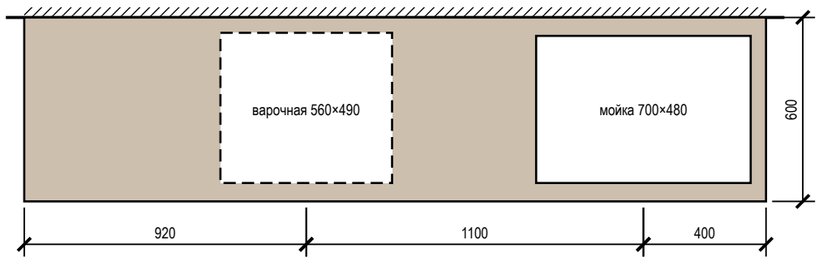


## Привязка выводов к осям модулей

| Код | Назначение | Модуль | От оси, мм | H, мм | Размещение |
|---|---|---|---|---|---|
| B1-2 | B1 — кран машины | M11** | −100 | 600 | в нише стиральной машины, за машиной (доступ — выдвинуть машину) |
| P20** | розетка — стиральная машина | M11** | 0 | 1100 | над столешницей (фартук) |
| K1-2 | K1 Ø40 — стиральная машина | M11** | +100 | 600 | в нише стиральной машины, за машиной (доступ — выдвинуть машину) |
| БП1 | блок питания | M11** | +210 | 2300 | над столешницей (фартук) |
| | вывод кабеля — варочная панель | M7 | 0 | 150 | в соседнем модуле, за ящиком |
| | розетка — вытяжка (встроена в дно M10) | M10 | 0 | 2200 | в навесном модуле |
| | розетка — рабочая зона | M6 | −100 | 1100 | над столешницей (фартук) |
| | розетка ×2 — рабочая зона | M6 | +100 | 1100 | над столешницей (фартук) |
| T3-1 | T3 — межос. 100 | M5 | −50 | 550 | в модуле мойки |
| K1-1 | K1 Ø50 — мойка | M5 | 0 | 400 | в модуле мойки |
| B1-1 | B1 — межос. 100 | M5 | +50 | 550 | в модуле мойки |
| | светодиодная лента — подсветка столешницы | M4 | −300 | 1400 | за пеналом |

## Зазоры под отделку

| Поверхность | Отделка | Зазор, мм | Учесть |
|---|---|---|---|
| фартук | плитка / стеновая панель | 10 | от чернового основания до корпуса навесных и столешницы |
| стены | окраска | 5 | под штукатурку и шпаклёвку за пеналом |
| пол | инженерная доска | | цоколь — после укладки пола, опоры ±20 мм |

## Условные обозначения

- нижний модуль, пенал (контур)
- невидимый контур: навесной модуль, корпус под столешницей
- ось модуля (от неё — привязка вывода)
- анкер / уголок крепления к стене
- розетка на стене
- вывод кабеля к технике
- B1 — вывод воды B1 / T3, канализации K1

**Допущения и предложения на листе**

Основа листа: размеры сняты с плана заказчика, контрольный обмер не выполнен (К-5); высота потолка 2700 мм принята: на плане заказчика не указана (К-5); подрайон климата не задан — принят не северный (жилые от 2,5 м) (К-4); толщины стен приняты: наружные 250 мм, перегородки 120 мм — не обмерены (К-5); разрешённая мощность 15 кВт принята по типовой квартире, технических условий нет (К-6).

Знак «**» — предложение проектировщика, заказчиком не утверждено (согласовать с заказчиком): К-7: M11 — место стиральной машины: вместо модуля с ящиками 400 справа от варочной; ряд до 3420, журнальный стол M21 (с х 3440) не мешает загрузке; P20 — питание стиральной машины П6 — отдельная группа 6 (УЗО 30 мА); над столешницей в габарите машины, не за корпусом.

См. лист открытых вопросов (лист 6, записи К-4–К-7).

## Примечания

1. Выводы — по проекту электрики и ВК; привязка по горизонтали — от оси модуля (плюс — вправо по виду), по высоте — от чистого пола до оси вывода.
2. Пенал — уголки к стене 2 шт. сверху; нижние модули — стяжками между собой и уголком к стене; ряд выставить по уровню опорами цоколя.
3. Розетки над столешницей — не ниже 150 мм над ней и не за корпусом техники; розетка за ПММ, духовым шкафом и холодильником — только в соседнем модуле или в зоне цоколя с доступом.
4. Столешница — вырезы по шаблонам выбранных моделей мойки и варочной панели; торцы у стены — герметик, пристеночный плинтус.

1000 мм · печать 1:1

| Изм. | Кол.уч | Лист | № док. | Подп. | Дата |
|---|---|---|---|---|---|
| Разраб. | | Кырлан А.С. | | | 04.11.26 |
| Пров. | | | | | |
| ГИП | | | | | |
| | | | | | |
| Н. контр. | | | | | |
| Утв. | | | | | |

**ГД-2026-006-АИ**

Квартира 58 м²

Общая площадь 55,23* м² · * размеры приняты, не замерены (реестр — л. 6, 7, К-5)

Дизайн-проект интерьера

| Стадия | Лист | Листов |
|---|---|---|
| РП | 56 | 87 |

**Кухня (пом. 1). Монтажная схема**

М 1:20

**Кырлан Александр Сергеевич**


выпуск 04.11.2026 № 3da8f16a26 · стр. 63 из 96

# Шкафы. Монтажная схема


крепление к стене, установочные размеры, зазоры под отделку · размеры в мм

ПРЕДВАРИТЕЛЬНО · не для производства работ · открыто пунктов: 10 (реестр — л. 6, 7)

**Шкаф-купе М9 (пом. 5)**

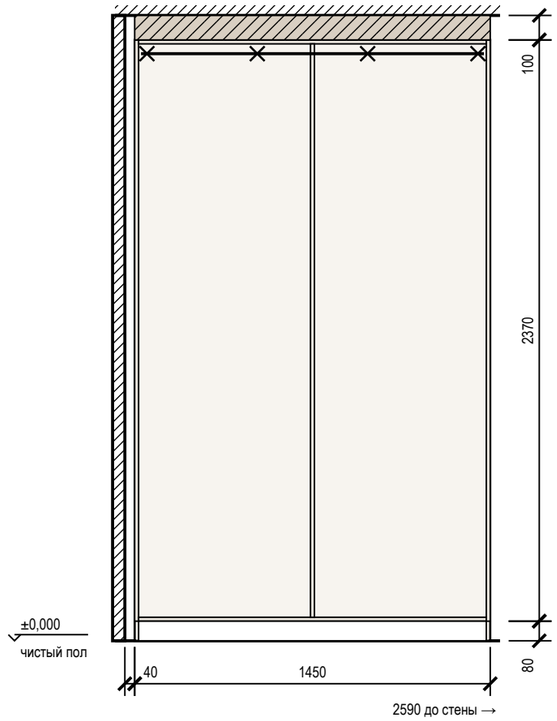


**Система хранения Г1 (пом. 6)**

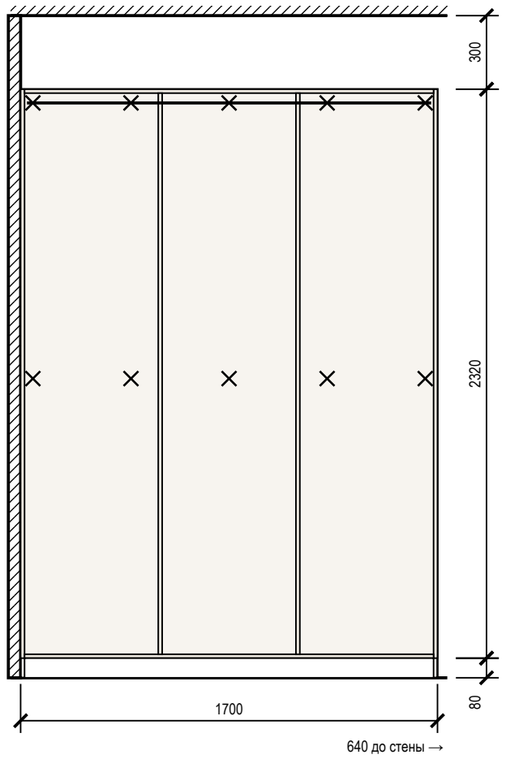


## Крепление и зазоры под отделку

| Марка | Помещение, стена | Основание | Отделка стены | Зазор, мм | Крепёж по планке | От опрокидывания |
|---|---|---|---|---|---|---|
| М9 | Прихожая (5), стена В | по основанию — см. таблицу крепежа | окраска | 5 | анкер 4 шт., шаг 450 | уголки 2 шт. |
| Г1 | Гардеробная (6), стена Б | по основанию — см. таблицу крепежа | окраска | 5 | анкер 10 шт. (2 ряда) | крепление к стене, 3 точки |

## Крепёж по основанию стены

| Основание стены | Крепёж |
|---|---|
| бетон, ж/б | анкер-шуруп 7,5×72 или дюбель 8×60 с шурупом 5×70 |
| кирпич полнотелый | дюбель 8×80 с шурупом 5×90 |
| газобетон, пазогребень | дюбель для газобетона 10×100 или химический анкер |
| гипсокартон | закладная до обшивки (брус 40×80 или фанера 18 мм), саморез в закладную |

## Условные обозначения

- анкер / уголок крепления к стене
- корпус и полки ЛДСП (вид на стену)
- компенсатор — короб до потолка

## Примечания

1. Установочные размеры — от чистого пола и чистых стен; перед установкой контрольный замер после отделки.
2. Порядок: корпус выставить по уровню опорами цоколя → закрепить к стене по задней планке → навесить двери и фасады, отрегулировать зазоры → подогнать и закрепить компенсатор.
3. Анкеры — с шагом не более 500 мм, не ближе 50 мм от края планки; на ГКЛ только в закладную, установленную до обшивки.
4. Скрытые коммуникации под анкеры проверить детектором; трассы электрики по плану розеток.

**Допущения и предложения на листе**

Основа листа: размеры сняты с плана заказчика, контрольный обмер не выполнен (К-5); высота потолка 2700 мм принята: на плане заказчика не указана (К-5); подрайон климата не задан — принят не северный (жилые от 2,5 м) (К-4); толщины стен приняты: наружные 250 мм, перегородки 120 мм — не обмерены (К-5); разрешённая мощность 15 кВт принята по типовой квартире, технических условий нет (К-6).
См. лист открытых вопросов (лист 6, записи К-4–К-6).

1000 мм · печать 1:1

| Изм. | Кол.уч | Лист | № док. | Подп. | Дата |
|---|---|---|---|---|---|
| Разраб. | | Кырлан А.С. | | | 04.11.26 |
| Пров. | | | | | |
| ГИП | | | | | |
| | | | | | |
| Н. контр. | | | | | |
| Утв. | | | | | |

**ГД-2026-006-АИ**

Квартира 58 м²

Общая площадь 55,23* м² · * размеры приняты, не замерены (реестр — л. 6, 7, К-5)

| Дизайн-проект интерьера | Стадия | Лист | Листов |
|---|---|---|---|
| | РП | 57 | 87 |
| **Шкафы. Монтажная схема** | **Кырлан Александр Сергеевич** | | |
| М 1:25 | | | |

выпуск 04.11.2026 № 3da8f16a26 · стр. 64 из 96

# Ведомости изделий, техники и фурнитуры

встроенная мебель и кухонный гарнитур · размеры в мм

## Ведомость изделий

| Марка | Наименование | Пом. | Ш×Г×В, мм | Корпус | Фасад | Кромка, мм | Кол. |
|---|---|---|---|---|---|---|---|
| М9 | Шкаф-купе | 5 | 1450×600×2450 | ЛДСП 16 | ЛДСП 10 мм в алюминиевом профиле | 0,4 / 1 | 1 |
| Г1 | Система хранения | 6 | 1700×600×2400 | ЛДСП 16 | без фасадов | 0,4 / 2 | 1 |
| М11** | Ниша под стиральную машину 620: без корпуса, между боковинами соседних модулей, фасад на петлях к боковине соседнего модуля; цоколь съёмный | 1 | 620×600×900 | без корпуса | МДФ эмаль 18 мм — на дверь машины (навеска из её комплекта), цоколь | | 1 |
| М7 | Модуль нижний: ящики, варочная | 1 | 600×600×900 | ЛДСП 16 | МДФ эмаль 18 мм | 0,4 / 1 | 1 |
| М10 | Модуль навесной: полки | 1 | 600×350×620 | ЛДСП 16 | МДФ эмаль 18 мм | 0,4 / 1 | 1 |
| М6 | Модуль нижний: ящики | 1 | 400×600×900 | ЛДСП 16 | МДФ эмаль 18 мм | 0,4 / 1 | 1 |
| М8 | Модуль навесной: полки, сушка | 1 | 1200×350×720 | ЛДСП 16 | МДФ эмаль 18 мм | 0,4 / 1 | 1 |
| М5 | Модуль нижний: мойка | 1 | 800×600×900 | ЛДСП 16 | МДФ эмаль 18 мм | 0,4 / 1 | 1 |
| М4 | Место под холодильник отдельностоящий: без корпуса и фасада | 1 | 600×650×2100 (место в ряду) | без корпуса | без фасада (прибор отдельностоящий) | | |

## Ведомость встраиваемой техники

| Поз. | Прибор | Ниша, вырез, мм | Вентиляция | Питание | Схема |
|---|---|---|---|---|---|
| М7 | Варочная панель индукционная, 60 см | вырез в столешнице 560 × 490 | | М7, Н=150 — в соседнем модуле, за ящиком | по модели |
| М5 | Мойка врезная / подстольная с сифоном | вырез по шаблону, ориентир 700 × 480 | | смеситель — выводы ВК | по модели |
| М4 | Холодильник отдельностоящий | проём 600, зазор сверху ≥ 50 | по паспорту модели | питание: точка ЭОМ не задана — вывод под прибор не делать до задания | по модели |
| М10 | Вытяжка встраиваемая в навесной модуль, 60 см | низ ≥ 650 над панелью | воздуховод к вентканалу, короб до потолка | питание: точка ЭОМ не задана — вывод под прибор не делать до задания | по модели |

## Ведомость фурнитуры

| № | Фурнитура | Тип, размер | Изделия | Кол. |
|---|---|---|---|---|
| 1 | Система дверей купе: профиль, направляющие, ролики | на 2 двери | М9 | 1 |
| 2 | Ручка-профиль вертикальная | в цвет профиля | М9 | 2 |
| 3 | Полкодержатель с фиксацией | ø5 мм | М9, Г1, М10, М8 | 56 |
| 4 | Штанга овальная 30×15, L = 701 | + 2 держателя | М9 | 1 |
| 5 | Полка для обуви выдвижная наклонная | ширина 701 | М9 | 3 |
| 6 | Опора регулируемая с цоколем на клипсах | ход 20 мм | М9, Г1 | 14 |
| 7 | Анкер по основанию стены | по таблице крепежа | М9, Г1, М10, М8 | 20 |
| 8 | Уголок крепления к стене от опрокидывания | стальной | М9, Г1 | 4 |
| 9 | Штанга овальная 30×15, L = 545 | + 2 держателя | Г1 | 3 |
| 10 | Петля накладная 110° с доводчиком | чашка 35 мм | М11**, М10, М8, М5 | 16 |
| 11 | Ручка-профиль | латунь матовая | М11**, М7, М10, М6, М8, М5 | 14 |
| 12 | Направляющие полного выдвижения с доводчиком NL 500 | пара | М7, М6 | 6 |
| 13 | Опора кухонная регулируемая 100–120 мм | + клипса цоколя | М7, М6, М5 | 14 |
| 14 | Навес регулируемый для навесного шкафа | пара на секцию | М10, М8 | 3 |
| 15 | Шина монтажная | L = 540 | М10 | 1 |
| 16 | Сушка для посуды в шкаф | ширина 800 | М8 | 1 |
| 17 | Шина монтажная | L = 1140 | М8 | 1 |

## Примечания

1. Модели техники выбирает заказчик до изготовления мебели; ниши, вырезы и вентиляция — по монтажной схеме выбранной модели (условие гарантии), её номер вносится в ведомость.
2. Количество фурнитуры — по чертежам изделий; запас крепежа 5 %. Аналоги — по характеристикам (доводчик, нагрузка, ход).
3. Цвет корпусов, фасадов и профилей — по колерной карте проекта. Кромка — скрытые / видимые торцы, мм.

**Допущения и предложения на листе**

Основа листа: размеры сняты с плана заказчика, контрольный обмер не выполнен (К-5); высота потолка 2700 мм принята: на плане заказчика не указана (К-5); подрайон климата не задан — принят не северный (жилые от 2,5 м) (К-4); толщины стен приняты: наружные 250 мм, перегородки 120 мм — не обмерены (К-5); разрешённая мощность 15 кВт принята по типовой квартире, технических условий нет (К-6).

Знак «**» — предложение проектировщика, заказчиком не утверждено (согласовать с заказчиком): К-7: М11 — место стиральной машины: вместо модуля с ящиками 400 справа от варочной; ряд до 3420, журнальный стол М21 (с х 3440) не мешает загрузке.

Изменения по листу без подписи: ИЗ-1.

См. лист открытых вопросов (лист 6, записи К-4–К-7; лист 7, запись ИЗ-1).

| Изм. | Кол.уч | Лист | № док. | Подп. | Дата |
|---|---|---|---|---|---|
| Разраб. | | Кырлан А.С. | | | 04.11.26 |
| Пров. | | | | | |
| ГИП | | | | | |
| Н. контр. | | | | | |
| Утв. | | | | | |

**ГД-2026-006-АИ**

Квартира 58 м²

Общая площадь 55,23* м² · * размеры приняты, не замерены (реестр — л. 6, 7, К-5)

Дизайн-проект интерьера

| Стадия | Лист | Листов |
|---|---|---|
| РП | 58 | 87 |

**Ведомости изделий, техники и фурнитуры**

М б/м

**Кырлан Александр Сергеевич**

выпуск 04.11.2026 № 3da8f16a26 · стр. 65 из 96

08

# Развёртки и узлы

Кырлан Александр Сергеевич

выпуск 04.11.2026 · 3da8f16a26 · стр. 66 из 96

# Реестр марок отделки и позиций альбома

Реестр марок отделки (О ↔ позиции колерной карты) и марки позиций по видам

## Реестр марок отделки альбома

| Марка | Поверхность | Материал, изделие | Цвет, код | Помещения | Колер. карта |
|---|---|---|---|---|---|
| О1 | стены | окраска, Tikkurila, шелковисто-матовая, подготовка Q3 | NCS S 1002-Y50R | 1 | К1 |
| О2 | плинтус | плинтус МДФ, Orac Decor Luxxus, h 110 мм, SX184, шелковисто-матовая | NCS S 0300-N | 1, 2, 5 | К3 |
| О3 | потолок | окраска, Tikkurila, глубокоматовая | NCS S 0300-N | 1, 2, 3, 4, 5 | К2, К5 |
| О4 | пол | инженерная доска, аналог: инженерная доска, дуб натуральный, масло, 1-полосная, 14/4 мм | | 1, 2, 6 | КМ1 |
| О5 | стены | окраска, Tikkurila, глубокоматовая, подготовка Q3 | NCS S 1502-Y50R | 2, 5 | К4, К6 |
| О6 | стены | облицовка плиткой, Italon Charme Extra, 600×1200 мм, 610015000370 | Italon 610015000370 «Charme Extra» | 3, 4 | КМ2 |
| О7 | пол | керамогранит, Kerama Marazzi Две Венеции / Риальто, 600×600 мм, SG651622R | Kerama Marazzi SG651622R «Две Венеции / Риальто» | 3, 4, 5 | КМ3 |
| О8 | стены | окраска, Tikkurila Harmony, матовая, подготовка Q3 | Tikkurila V503 «Winter» | 6 | К7 |
| О9 | плинтус | плинтус МДФ, Orac Decor Luxxus, h 110 мм, SX184 | Tikkurila V503 «Winter» | 6 | К9 |
| О10 | потолок | окраска, Tikkurila Anti-Reflex 2, глубокоматовая, подготовка Q3 | Tikkurila V503 «Winter» | 6 | К8 |

## Марки позиций альбома по видам

| Префикс | Что обозначает, позиции | Листы |
|---|---|---|
| Д | двери: Д-1–Д-4 | 14–16 |
| ОК | окна: ОК-1 | 14–16 |
| Г, М, С | мебель и оборудование: Г1, М1**, М3–М10, М11**, М20, М21, М22**, С1–С3 | 17–19 |
| П | сантехнические приборы: П1**, П3**, П4, П5, П6**, П20 | 29–38 |
| Р | розетки: Р1–Р16, Р20** | 20–26 |
| ЭВ | выводы кабеля: ЭВ1–ЭВ3 | 20–26 |
| S | выключатели: S1–S9 | 20–26 |
| Св | светильники: Св1**, Св2**, Св3, Св4, Св5**, Св6–Св8, Св9**, Св10–Св12, Св16 | 20–26 |
| ИП | извещатели: ИП1–ИП3 | 20–26 |
| ТВ | розетки ТВ: ТВ1 | 20–26 |
| LAN | розетки компьютерные: LAN1, LAN2 | 20–26 |
| БП | блоки питания LED: БП1, БП2 | 20–26 |
| КУП | электроустановочные изделия: КУП1 | 20–26 |
| ЩК, ЩС** | щиты: ЩК, ЩС** | 20–26 |
| ДФ | домофон: ДФ1 | 20–26 |
| Ст В1, Ст К1, Ст Т3 | стояки (системы В1, Т3, К1): Ст В1-1, Ст К1-1, Ст Т3-1 | 29–38 |
| Ш | шахты и короба: Ш1 | 14–16 |

## Марки позиций альбома по видам (продолжение)

| Префикс | Что обозначает, позиции | Листы |
|---|---|---|
| О | марки отделки (реестр альбома): О1–О10 | 2–5, 59–80 |
| К, КМ | позиции колерной карты: К1–К9, КМ1–КМ3 | 49, 50 |
| Р | радиаторы отопления: Р-1–Р-3 | 27, 28 |

## Примечания

1. Марка отделки О — одна на весь альбом: одна и та же отделка (материал, изделие, цвет, формат) на всех листах имеет одну марку; на развёртках и планах стоят марки этого реестра.
2. Столбец «Колер. карта» — позиции колерной карты (лист 49): К — окраска по коду цвета, КМ — материал без кода цвета; «Помещения» — номера по экспликации; количества — по ведомости отделки помещений (лист 48).
3. Марки позиций: один префикс — один вид позиций на весь альбом (двери Д, окна ОК, мебель М, сантехприборы П, декор ДК, текстиль Т, колерная карта К и КМ, радиаторы РО, розетки Р, выключатели S, светильники Св; стояки — «Ст» и система, например «Ст К1-1»). Совпадение префиксов у разных видов — замечание к исходным данным, при выпуске исправляется в модели.

**Допущения и предложения на листе**

Основа листа: размеры сняты с плана заказчика, контрольный обмер не выполнен (К-5); высота потолка 2700 мм принята: на плане заказчика не указана (К-5); подрайон климата не задан — принят не северный (жилые от 2,5 м) (К-4); толщины стен приняты: наружные 250 мм, перегородки 120 мм — не обмерены (К-5); разрешённая мощность 15 кВт принята по типовой квартире, технических условий нет (К-6).

Знак «**» — предложение проектировщика, заказчиком не утверждено (согласовать с заказчиком): Св2 — общий свет зоны гостиной над журнальным столом М21 (трек шёл вдоль края стола М3 по проходу); трековая система 4 × 950 лм: поток принят до нормы освещённости, модель и паспорт не выбраны; Св5 — трековая система 2 × 900 лм: светильник добавлен проектировщиком, поток принят до нормы освещённости, модель и паспорт не выбраны; Св1 — подвес висел над проходом без заданной высоты, а стол — без света над ним: подвес по оси стола М3; Св9 — свет у зеркала — над зеркалом у умывальника по его оси (свет на лицо, а не над сантехникой); ЩС — щит слаботочный: место и состав; пол пом. 1, 2, 6 — артикул изделия не выбран: позиция описана характеристиками («аналог по характеристикам»), артикул выбирается при закупке; ИЗ-2: М1 — Было offset 1300…3500: торец дивана в 500 мм от стены В, правые 350 мм проёма Д-2 (3900…4800) упирались в диван; М22 — Было х 4250 — место занял диван М1 (х 4450…5400 от у 1000); К-2: П1 — ванна 1500 вместо 1600 — не заходит в проход перед проёмом Д-4; перед ванной 680 мм — глубина помещения; П3 — умывальник у стены В справа от ванны — перед ним свободно 750 мм, до стены Б 90 мм; К-7: М11 — место стиральной машины: вместо модуля с ящиками 400 справа от варочной; ряд до 3420, журнальный стол М21 (с х 3440) не мешает загрузке; П6 — стиральная машина на кухне: в ванной и санузле места нет; подвод ХВС с шаровым краном, слив — встраиваемый сифон с обратным клапаном (водяной затвор), отдельная группа 6 щита с УЗО 30 мА; Р20 — питание стиральной машины П6 — отдельная группа 6 (УЗО 30 мА); над столешницей в габарите машины, не за корпусом.

См. лист открытых вопросов (лист 6, записи К-2, К-4–К-7; лист 7, запись ИЗ-2).

| | | | | | |
|---|---|---|---|---|---|
| | | | | | |
| | | | | | |
| | | | | | |
| Изм. | Кол.уч | Лист | № док. | Подп. | Дата |
| Разраб. | | Кырлан А.С. | | | 04.11.26 |
| Пров. | | | | | |
| ГИП | | | | | |
| | | | | | |
| Н. контр. | | | | | |
| Утв. | | | | | |

**ГД-2026-006-АИ**

Квартира 58 м²

Общая площадь 55,23* м² · * размеры приняты, не замерены (реестр — л. 6, 7, К-5)

Дизайн-проект интерьера

| Стадия | Лист | Листов |
|---|---|---|
| РП | 59 | 87 |

**Реестр марок отделки и позиций альбома**

М б/м

**Кырлан Александр Сергеевич**

# Схема расположения развёрток и узлов

План квартиры: марки развёрток по помещениям, выноски узлов, ведомость «марка → лист»

ПРЕДВАРИТЕЛЬНО · не для производства работ · открыто пунктов: 10 (реестр — л. 6, 7)




## Развёртки и узлы: марка → лист

| Марка | Помещение / узел | Лист |
|---|---|---|
| В | Кухня-гостиная (пом. 1) | 61, 62 |
| А | Кухня-гостиная (пом. 1) | 63 |
| Б | Кухня-гостиная (пом. 1) | 64 |
| Г | Кухня-гостиная (пом. 1) | 65 |
| А | Спальня (пом. 2) | 66 |
| Б | Спальня (пом. 2) | 67, 68 |
| В | Спальня (пом. 2) | 69 |
| А, Б, В | Ванная (пом. 3) | 70, 71 |
| Г | Ванная (пом. 3) | 72 |
| А, Б, В | Санузел (пом. 4) | 73 |
| Г | Санузел (пом. 4) | 74 |
| А, Б | Прихожая (пом. 5) | 75 |
| В, Г | Прихожая (пом. 5) | 76, 77 |
| А, Б | Гардеробная (пом. 6) | 78 |
| Г | Гардеробная (пом. 6) | 79 |
| узел 1 | Порог 15 мм: мокрая зона — смежное помещение | 80 |
| узел 2 | Дверь скрытого монтажа в плоскости стены, плинтус | 80 |
| узел 3 | Короб стояков К1-1 с люком и звукоизоляцией | 80 |
| узел 4 | Гидроизоляция санузла: заход на стены 200 мм, примыкание ванны | 80 |
| узел 5 | Плинтус МДФ 110×16 мм у окрашенной стены по доске (ламинату) | 80 |
| узел 6 | Плинтус МДФ 110×16 мм у окрашенной стены по керамограниту (плитке) | 80 |

## Условные обозначения

- А — марка развёртки: буква стены, стрелка — взгляд
- выноска узла: над полкой — узел, под полкой — лист
- 1 — номер помещения, площадь м²

1000 мм · печать 1:1

## Примечания

1. Развёртки — вид на стену изнутри помещения; буквы стен — одна система на весь альбом (как на листах выводов, плитки и отделки).
2. Стены без электроточек, мебели, декора и акцентной отделки развёрток не имеют: их отделка — по ведомости отделки помещений.
3. Узлы — на листе узлов; места применения — по выноскам этого листа и ведомости «марка → лист».

**Допущения и предложения на листе**

Основа листа: размеры сняты с плана заказчика, контрольный обмер не выполнен (К-5); высота потолка 2700 мм принята: на плане заказчика не указана (К-5); подрайон климата не задан — принят не северный (жилые от 2,5 м) (К-4); толщины стен приняты: наружные 250 мм, перегородки 120 мм — не обмерены (К-5); разрешённая мощность 15 кВт принята по типовой квартире, технических условий нет (К-6).
См. лист открытых вопросов (лист 6, записи К-4–К-6).

| Изм. | Кол.уч | Лист | № док. | Подп. | Дата |
|---|---|---|---|---|---|
| Разраб. | | Кырлан А.С. | | | 04.11.26 |
| Пров. | | | | | |
| ГИП | | | | | |
| | | | | | |
| Н. контр. | | | | | |
| Утв. | | | | | |

**ГД-2026-006-АИ**

Квартира 58 м²

Общая площадь 55,23* м² · * размеры приняты, не замерены (реестр — л. 6, 7, К-5)

Дизайн-проект интерьера

| Стадия | Лист | Листов |
|---|---|---|
| РП | 60 | 87 |

**Схема расположения развёрток и узлов**

М 1:50

**Кырлан Александр Сергеевич**


выпуск 04.11.2026 № 3da8f16a26 · стр. 68 из 96

# Развёртка стены В. Кухня-гостиная (пом. 1), кухонный фронт

Кухня-гостиная (пом. 1) · вид изнутри помещения · размеры в мм, отметки в м


ПРЕДВАРИТЕЛЬНО · не для производства работ · открыто пунктов: 10 (реестр — л. 6, 7)

## Развёртка стены В

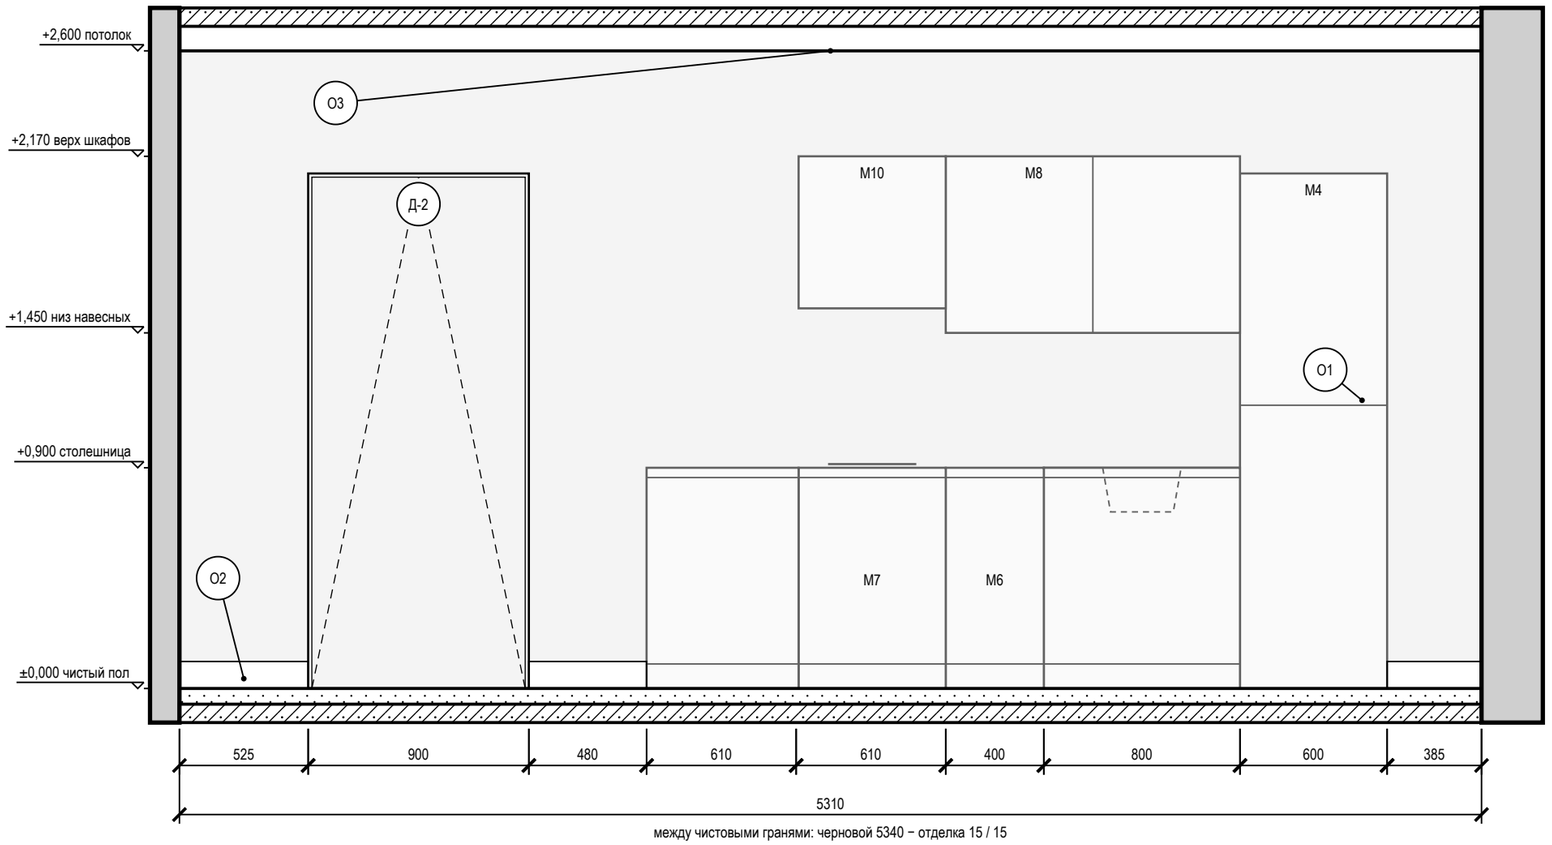


между чистовыми гранями: черновой 5340 − отделка 15 / 15

## Схема развёрток (М 1:100)

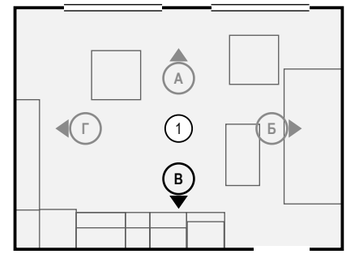


## Условные обозначения

- мебель и приборы — фасад по расстановке (условно)
- дверь скрытого монтажа: полотно в плоскости стены (узел — на листе узлов)
- стены и перекрытия в сечении
- О1 — марка отделки по реестру отделки альбома
- А — марка развёртки: буква стены, стрелка — взгляд

## Ведомость отделки (на листе)

| Марка | Поверхность | Материал, изделие | Цвет, код | Кол. |
|---|---|---|---|---|
| О1 | стены | окраска, Tikkurila, шелковисто-матовая, подготовка Q3 | NCS S 1002-Y50R | 11,9 м² |
| О2 | плинтус | плинтус МДФ, Orac Decor Luxxus, h 110 мм, SX184, шелковисто-матовая | NCS S 0300-N | 1,4 м |
| О3 | потолок | окраска, Tikkurila, глубокоматовая | NCS S 0300-N | 21 м² |

## Примечания

1. Развёртки — вид на стену изнутри помещения, по часовой стрелке; расположение — на схеме листа и на листе 60; размеры — в мм по чистовым поверхностям; отметки — в м от ±0,000; высоты Н — от чистого пола помещения до оси изделия, у декора — до центра.
2. Стена В показана двумя видами: здесь — архитектурная развёртка (мебель, отделка, проёмы, высоты), электроточки и выводы ВК с привязками и таблицей — на листе 62 («Привязки»).
3. Схема мебели, приборов и декора не является технической документацией для производства мебели; габариты — по паспортам изделий.
4. Двери скрытого монтажа — полотно в плоскости стены, отделка стены по полотну, плинтус прерывается у короба (узел — на листе узлов).
5. Потолок — у каждой стены свой, по плану потолков (ПТ2); ступени — зоной, кромка короба перед нишей — тонкой линией; в поле потолка: ПТ1 +2,550.

**Допущения и предложения на листе**

Основа листа: размеры сняты с плана заказчика, контрольный обмер не выполнен (К-5); высота потолка 2700 мм принята: на плане заказчика не указана (К-5); подрайон климата не задан — принят не северный (жилые от 2,5 м) (К-4); толщины стен приняты: наружные 250 мм, перегородки 120 мм — не обмерены (К-5); разрешённая мощность 15 кВт принята по типовой квартире, технических условий нет (К-6).
См. лист открытых вопросов (лист 6, записи К-4–К-6).

1000 мм · печать 1:1

| Изм. | Кол.уч | Лист | № док. | Подп. | Дата |
|---|---|---|---|---|---|
| Разраб. | | Кырлан А.С. | | | 04.11.26 |
| Пров. | | | | | |
| ГИП | | | | | |
| | | | | | |
| Н. контр. | | | | | |
| Утв. | | | | | |

**ГД-2026-006-АИ**

Квартира 58 м²

Общая площадь 55,23* м² · * размеры приняты, не замерены (реестр — л. 6, 7, К-5)

Дизайн-проект интерьера

| Стадия | Лист | Листов |
|---|---|---|
| РП | 61 | 87 |

**Развёртка стены В. Кухня-гостиная (пом. 1), кухонный фронт**
М 1:25

**Кырлан Александр Сергеевич**


выпуск 04.11.2026 № 3da8f16a26 · стр. 69 из 96

# Привязки электроточек и выводов ВК, стена В. Кухня-гостиная (пом. 1)

Кухня-гостиная (пом. 1) · вид изнутри помещения · привязки в мм, отметки в м · к развёртке на листе 61

ПРЕДВАРИТЕЛЬНО · не для производства работ · открыто пунктов: 10 (реестр — л. 6, 7)


## Развёртка стены В: электроточки и выводы

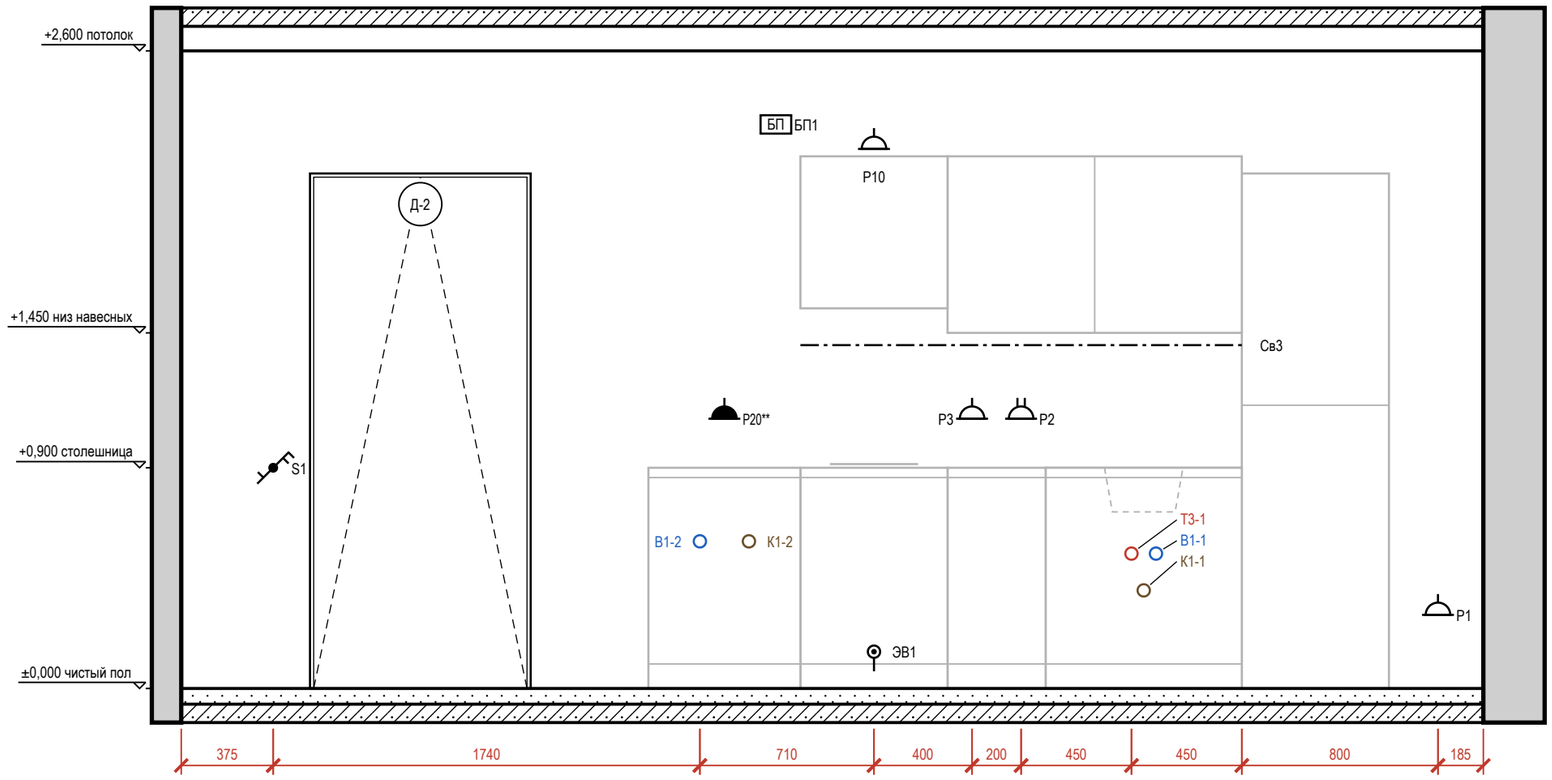


## Условные обозначения

- розетка с заземляющим контактом; у знака — марка, ×N постов в рамке, гр. — группа щита, H — высота оси, мм
- розетка влагозащищённая IP44
- вывод кабеля для подключения прибора (без розетки), марка ЭВ
- выключатель одноклавишный
- выключатель двухклавишный (флажков — по числу клавиш)
- выключатель с проходной или перекрёстной клавишей (обратный флажок); тип клавиши — в подписи
- светодиодная лента в профиле / в карнизе короба
- БП — блок питания LED, с доступом (люк от 100×100 мм)
- вывод В1 (код — в ведомости привязок)
- вывод Т3 (код — в ведомости привязок)
- вывод К1 (код — в ведомости привязок)
- привязки точек и выводов от угла и от пола, мм
- А — марка развёртки: буква стены, стрелка — взгляд

## Схема развёрток (М 1:100)

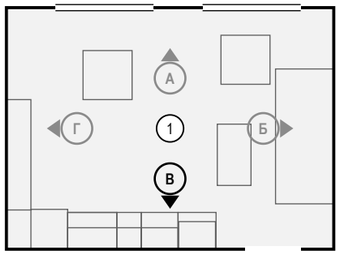


## Таблица привязок электроточек и выводов

| Марка | Назначение | От угла, мм | H от пола, мм | Примечание |
|---|---|---|---|---|
| S1 | выключатель | 375 | 900 | гр. 1 |
| В1-2 | холодная вода — стиральная машина | 2115 | 600 | кран машины |
| Р20** | розетка: стиральная машина | 2215 | 1100 | гр. 6, IP44 |
| К1-2 | канализация — стиральная машина | 2315 | 600 | Ø40 |
| БП1 | блок питания LED | 2425 | 2300 | гр. 1 |
| ЭВ1 | вывод кабеля: варочная панель | 2825 | 150 | гр. 3 |
| Р10 | розетка: вытяжка (встроена в дно М10) | 2825 | 2200 | гр. 2 |

| Марка | Назначение | От угла, мм | H от пола, мм | Примечание |
|---|---|---|---|---|
| Р3 | розетка: рабочая зона | 3225 | 1100 | гр. 2 |
| Р2 | розетка: рабочая зона | 3425 | 1100 | рамка 2 поста, гр. 2 |
| Т3-1 | горячая вода — мойка кухонная | 3875 | 550 | межос. 100 |
| К1-1 | канализация — мойка кухонная | 3925 | 400 | Ø50 |
| В1-1 | холодная вода — мойка кухонная | 3975 | 550 | межос. 100 |
| Св3 | светильник настенный | 4325 | 1400 | гр. 1, лента 2525–4325 от угла |
| Р1 | розетка: холодильник | 5125 | 300 | гр. 2 |

**Допущения и предложения на листе**

Основа листа: размеры сняты с плана заказчика, контрольный обмер не выполнен (К-5); высота потолка 2700 мм принята: на плане заказчика не указана (К-5); подрайон климата не задан — принят не северный (жилые от 2,5 м) (К-4); толщины стен приняты: наружные 250 мм, перегородки 120 мм — не обмерены (К-5); разрешённая мощность 15 кВт принята по типовой квартире, технических условий нет (К-6).

Знак «**» — предложение проектировщика, заказчиком не утверждено (согласовать с заказчиком): К-7: Р20 — питание стиральной машины П6 — отдельная группа 6 (УЗО 30 мА); над столешницей в габарите машины, не за корпусом.

См. лист открытых вопросов (лист 6, записи К-4–К-7).

## Примечания

1. Вид «Привязки» стены В — электроточки и выводы ВК; архитектурная развёртка (мебель, отделка, проёмы, высоты) — на листе 61, расположение — на листе 60. Мебель и приборы — подложкой для ориентира; их марки и обозначения мебели, проёмов и стен — там же.
2. Привязки — в мм: по горизонтали от левого чистового угла стены до оси изделия, H — от чистого пола до оси; все точки — в таблице привязок. Красная цепочка — привязки по осям; точки ближе 150 мм одна к другой в цепочку не дробятся — их привязки только в таблице.
3. У знака — марка электроточки (Р — розетка, S — выключатель, Св — светильник, ЭВ — вывод кабеля); посты в рамке и группа щита — в графе «Примечание»; группы по клавишам выключателя — на листе выключателей.
4. Коды выводов ВК: В1 — холодная вода, Т3 — горячая вода, К1 — канализация; номер после дефиса — номер вывода на листе выводов сантехники.
5. Выводы кухонной техники — по утверждённому проекту кухни: привязки выводов даются от осей модулей гарнитура.

1000 мм · печать 1:1

| Изм. | Кол.уч | Лист | № док. | Подп. | Дата |
|---|---|---|---|---|---|
| Разраб. | | Кырлан А.С. | | | 04.11.26 |
| Пров. | | | | | |
| ГИП | | | | | |
| | | | | | |
| Н. контр. | | | | | |
| Утв. | | | | | |

**ГД-2026-006-АИ**

Квартира 58 м²

Общая площадь 55,23* м² · * размеры приняты, не замерены (реестр — л. 6, 7, К-5)

Дизайн-проект интерьера

| Стадия | Лист | Листов |
|---|---|---|
| РП | 62 | 87 |

**Привязки электроточек и выводов ВК, стена В. Кухня-гостиная (пом. 1)**

М 1:25

**Кырлан Александр Сергеевич**


выпуск 04.11.2026 № 3da8f16a26 · стр. 70 из 96

# Развёртка стены А. Кухня-гостиная (пом. 1)

Кухня-гостиная (пом. 1) · вид изнутри помещения · размеры в мм, отметки в м


ПРЕДВАРИТЕЛЬНО · не для производства работ · открыто пунктов: 10 (реестр — л. 6, 7)

## Развёртка стены А

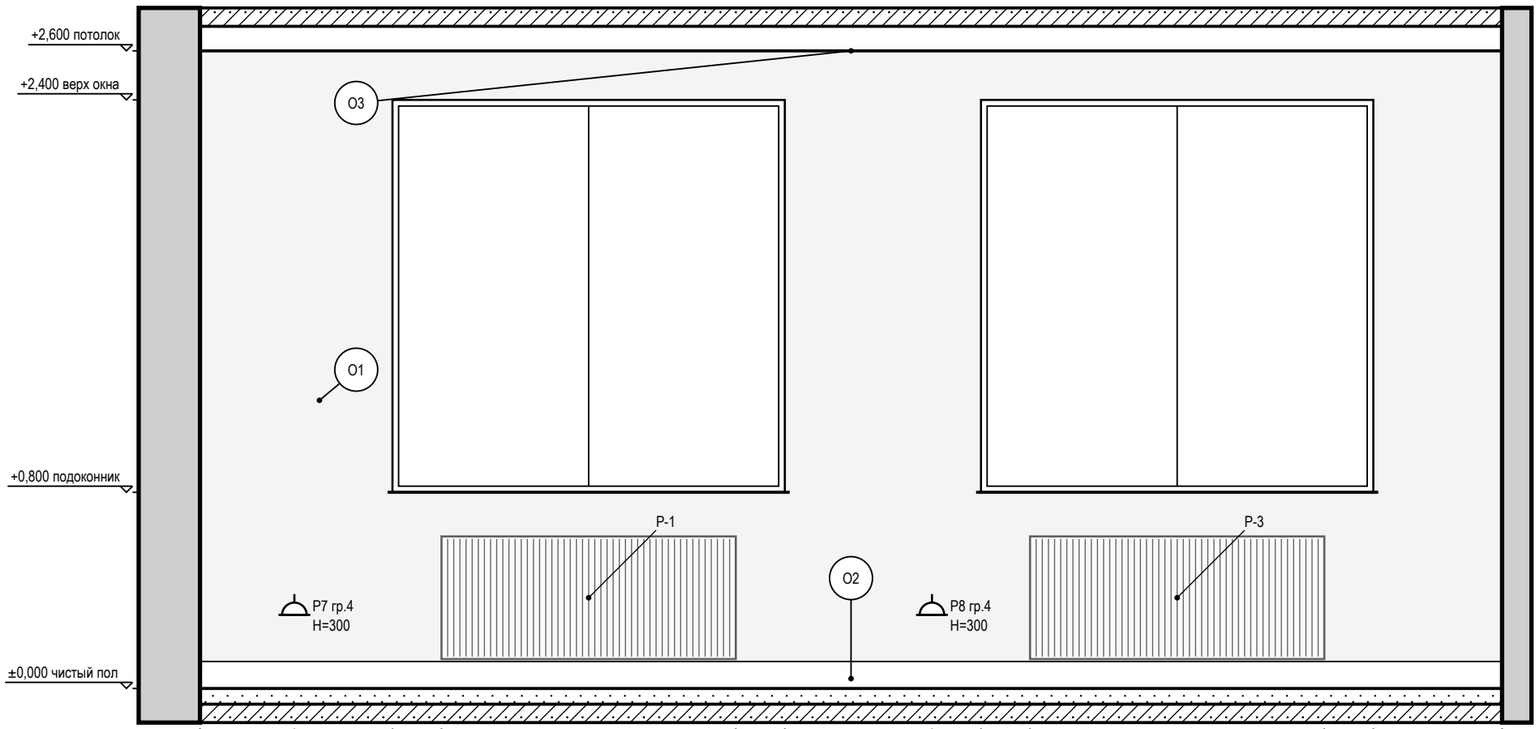


между чистовыми гранями: черновой 5340 − отделка 15 / 15

## Схема развёрток (М 1:100)

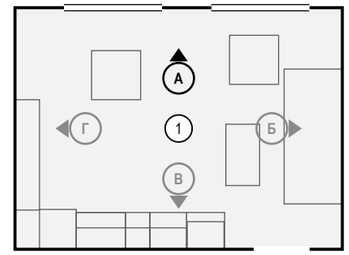


## Условные обозначения

- розетка с заземляющим контактом; у знака — марка, ×N постов в рамке, гр. — группа щита, Н — высота оси, мм
- привязки точек и выводов от угла и от пола, мм
- мебель и приборы — фасад по расстановке (условно)
- окно: проём, рама, подоконник
- радиатор отопления; марка — по плану отопления
- стены и перекрытия в сечении
- О1 — марка отделки по реестру отделки альбома
- А — марка развёртки: буква стены, стрелка — взгляд

## Ведомость отделки (на листе)

| Марка | Поверхность | Материал, изделие | Цвет, код | Кол. |
|---|---|---|---|---|
| О1 | стены | окраска, Tikkurila, шелковисто-матовая, подготовка Q3 | NCS S 1002-Y50R | 8,7 м² |
| О2 | плинтус | плинтус МДФ, Orac Decor Luxxus, h 110 мм, SX184, шелковисто-матовая | NCS S 0300-N | 5,3 м |
| О3 | потолок | окраска, Tikkurila, глубокоматовая | NCS S 0300-N | 21 м² |

**Допущения и предложения на листе**

Основа листа: размеры сняты с плана заказчика, контрольный обмер не выполнен (К-5); высота потолка 2700 мм принята: на плане заказчика не указана (К-5); подрайон климата не задан — принят не северный (жилые от 2,5 м) (К-4); толщины стен приняты: наружные 250 мм, перегородки 120 мм — не обмерены (К-5); разрешённая мощность 15 кВт принята по типовой квартире, технических условий нет (К-6).

См. лист открытых вопросов (лист 6, записи К-4–К-6).

## Примечания

1. Развёртки — вид на стену изнутри помещения, по часовой стрелке; расположение — на схеме листа и на листе 60; размеры — в мм по чистовым поверхностям; отметки — в м от ±0,000; высоты Н — от чистого пола помещения до оси изделия, у декора — до центра.
2. Красная цепочка — привязки электроточек и выводов по осям от угла чистовых стен; высота Н — у знака, от чистого пола до оси; высоты мебели, проёмов и границ отделки — колонкой отметок слева. Стена с 5 и более точками или с мелкими звеньями привязок показана двумя видами: архитектурная развёртка (мебель, отделка, проёмы, высоты) и вид «Привязки» на отдельном листе — точки и выводы с марками, одна цепочка по осям и таблица привязок (каждая точка — строка).
3. У знака электроточки: марка (Р — розетка, S — выключатель, Св — светильник, ЭВ — вывод кабеля), ×N — число постов в рамке, гр. — группа щита, Н — высота оси от чистого пола, мм; группы по клавишам выключателя — на листе выключателей.
4. Схема мебели, приборов и декора не является технической документацией для производства мебели; габариты — по паспортам изделий.
5. Потолок — у каждой стены свой, по плану потолков (ПТ2); ступени — зоной, кромка короба перед нишей — тонкой линией; в поле потолка: ПТ1 +2,550.

1000 мм · печать 1:1

| Изм. | Кол.уч | Лист | № док. | Подп. | Дата |
|---|---|---|---|---|---|
| Разраб. | | Кырлан А.С. | | | 04.11.26 |
| Пров. | | | | | |
| ГИП | | | | | |
| | | | | | |
| Н. контр. | | | | | |
| Утв. | | | | | |

**ГД-2026-006-АИ**

Квартира 58 м²

Общая площадь 55,23* м² · * размеры приняты, не замерены (реестр — л. 6, 7, К-5)

Дизайн-проект интерьера

| Стадия | Лист | Листов |
|---|---|---|
| РП | 63 | 87 |

**Развёртка стены А. Кухня-гостиная (пом. 1)**

М 1:25

**Кырлан Александр Сергеевич**


выпуск 04.11.2026 № 3da8f16a26 · стр. 71 из 96

# Развёртка стены Б. Кухня-гостиная (пом. 1)

Кухня-гостиная (пом. 1) · вид изнутри помещения · размеры в мм, отметки в м

ПРЕДВАРИТЕЛЬНО · не для производства работ · открыто пунктов: 10 (реестр — л. 6, 7)

## Развёртка стены Б

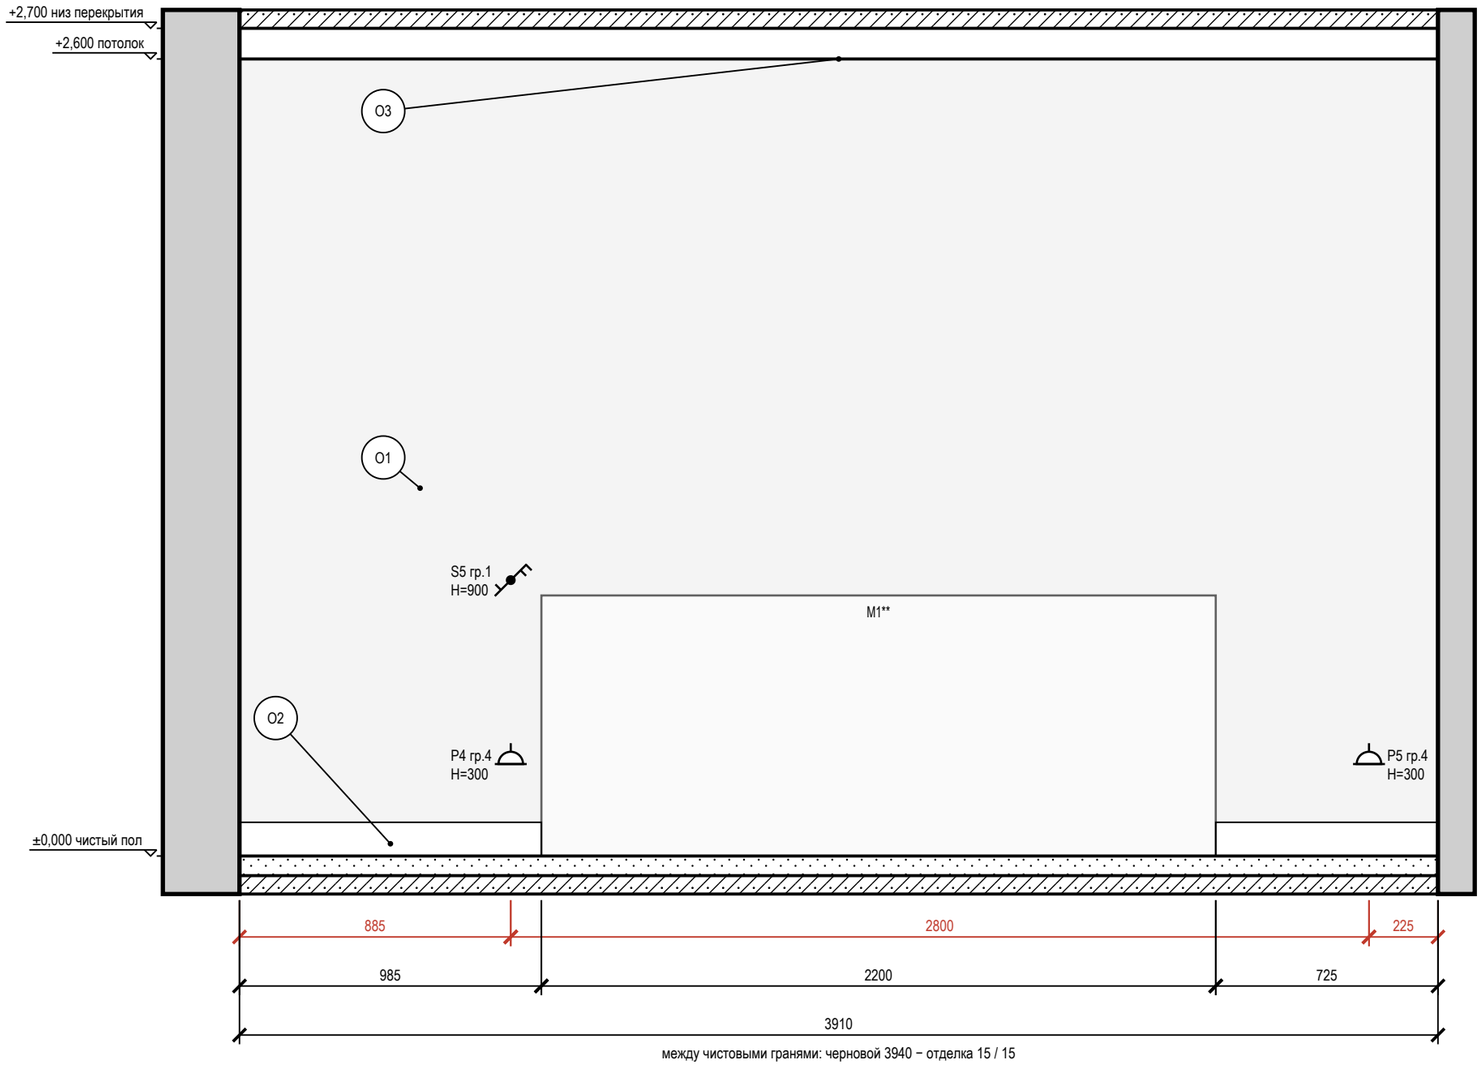


между чистовыми гранями: черновой 3940 − отделка 15 / 15

**Допущения и предложения на листе**

Основа листа: размеры сняты с плана заказчика, контрольный обмер не выполнен (К-5); высота потолка 2700 мм принята: на плане заказчика не указана (К-5); подрайон климата не задан — принят не северный (жилые от 2,5 м) (К-4); толщины стен приняты: наружные 250 мм, перегородки 120 мм — не обмерены (К-5); разрешённая мощность 15 кВт принята по типовой квартире, технических условий нет (К-6).

Знак «**» — предложение проектировщика, заказчиком не утверждено (согласовать с заказчиком): И3-2: М1 — Было offset 1300…3500: торец дивана в 500 мм от стены В, правые 350 мм проёма Д-2 (3900…4800) упирались в диван.


См. лист открытых вопросов (лист 6, записи К-4–К-6; лист 7, запись И3-2).

## Примечания

1. Развёртки — вид на стену изнутри помещения, по часовой стрелке; расположение — на схеме листа и на листе 60; размеры — в мм по чистовым поверхностям; отметки — в м от ±0,000; высоты Н — от чистого пола помещения до оси изделия, у декора — до центра.
2. Красная цепочка — привязки электроточек и выводов по осям от угла чистовых стен; высота Н — у знака, от чистого пола до оси; высоты мебели, проёмов и границ отделки — колонкой отметок слева. Стена с 5 и более точками или с мелкими звеньями привязок показана двумя видами: архитектурная развёртка (мебель, отделка, проёмы, высоты) и вид «Привязки» на отдельном листе — точки и выводы с марками, одна цепочка по осям и таблица привязок (каждая точка — строка).
3. У знака электроточки: марка (Р — розетка, S — выключатель, Св — светильник, ЭВ — вывод кабеля), ×N — число постов в рамке, гр. — группа щита, Н — высота оси от чистого пола, мм; группы по клавишам выключателя — на листе выключателей.
4. Схема мебели, приборов и декора не является технической документацией для производства мебели; габариты — по паспортам изделий.
5. Потолок — у каждой стены свой, по плану потолков (ПТ2); ступени — зоной, кромка короба перед нишей — тонкой линией; в поле потолка: ПТ1 +2,550.

1000 мм · печать 1:1

## Схема развёрток (М 1:100)

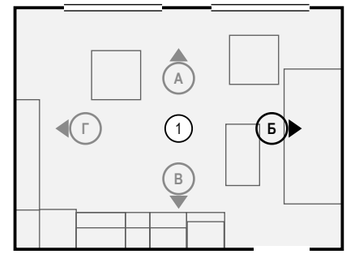


## Условные обозначения

- розетка с заземляющим контактом; у знака — марка, ×N постов в рамке, гр. — группа щита, Н — высота оси, мм
- выключатель одноклавишный
- выключатель двухклавишный (флажков — по числу клавиш)
- выключатель с проходной или перекрёстной клавишей (обратный флажок); тип клавиши — в подписи
- привязки точек и выводов от угла и от пола, мм
- мебель и приборы — фасад по расстановке (условно)
- стены и перекрытия в сечении
- О1 — марка отделки по реестру отделки альбома
- А — марка развёртки: буква стены, стрелка — взгляд

## Ведомость отделки (на листе)

| Марка | Поверхность | Материал, изделие | Цвет, код | Кол. |
|---|---|---|---|---|
| О1 | стены | окраска, Tikkurila, шелковисто-матовая, подготовка Q3 | NCS S 1002-Y50R | 10,2 м² |
| О2 | плинтус | плинтус МДФ, Orac Decor Luxxus, h 110 мм, SX184, шелковисто-матовая | NCS S 0300-N | 1,7 м |
| О3 | потолок | окраска, Tikkurila, глубокоматовая | NCS S 0300-N | 21 м² |

| Изм. | Кол.уч | Лист | № док. | Подп. | Дата |
|---|---|---|---|---|---|
| Разраб. | | Кырлан А.С. | | | 04.11.26 |
| Пров. | | | | | |
| ГИП | | | | | |
| | | | | | |
| Н. контр. | | | | | |
| Утв. | | | | | |

**ГД-2026-006-АИ**

Квартира 58 м²

Общая площадь 55,23* м² · * размеры приняты, не замерены (реестр — л. 6, 7, К-5)

Дизайн-проект интерьера

| Стадия | Лист | Листов |
|---|---|---|
| РП | 64 | 87 |

**Развёртка стены Б. Кухня-гостиная (пом. 1)**

М 1:20

**Кырлан Александр Сергеевич**


выпуск 04.11.2026 № 3da8f16a26 · стр. 72 из 96

# Развёртка стены Г. Кухня-гостиная (пом. 1)


Кухня-гостиная (пом. 1) · вид изнутри помещения · размеры в мм, отметки в м

ПРЕДВАРИТЕЛЬНО · не для производства работ · открыто пунктов: 10 (реестр — л. 6, 7)

## Развёртка стены Г

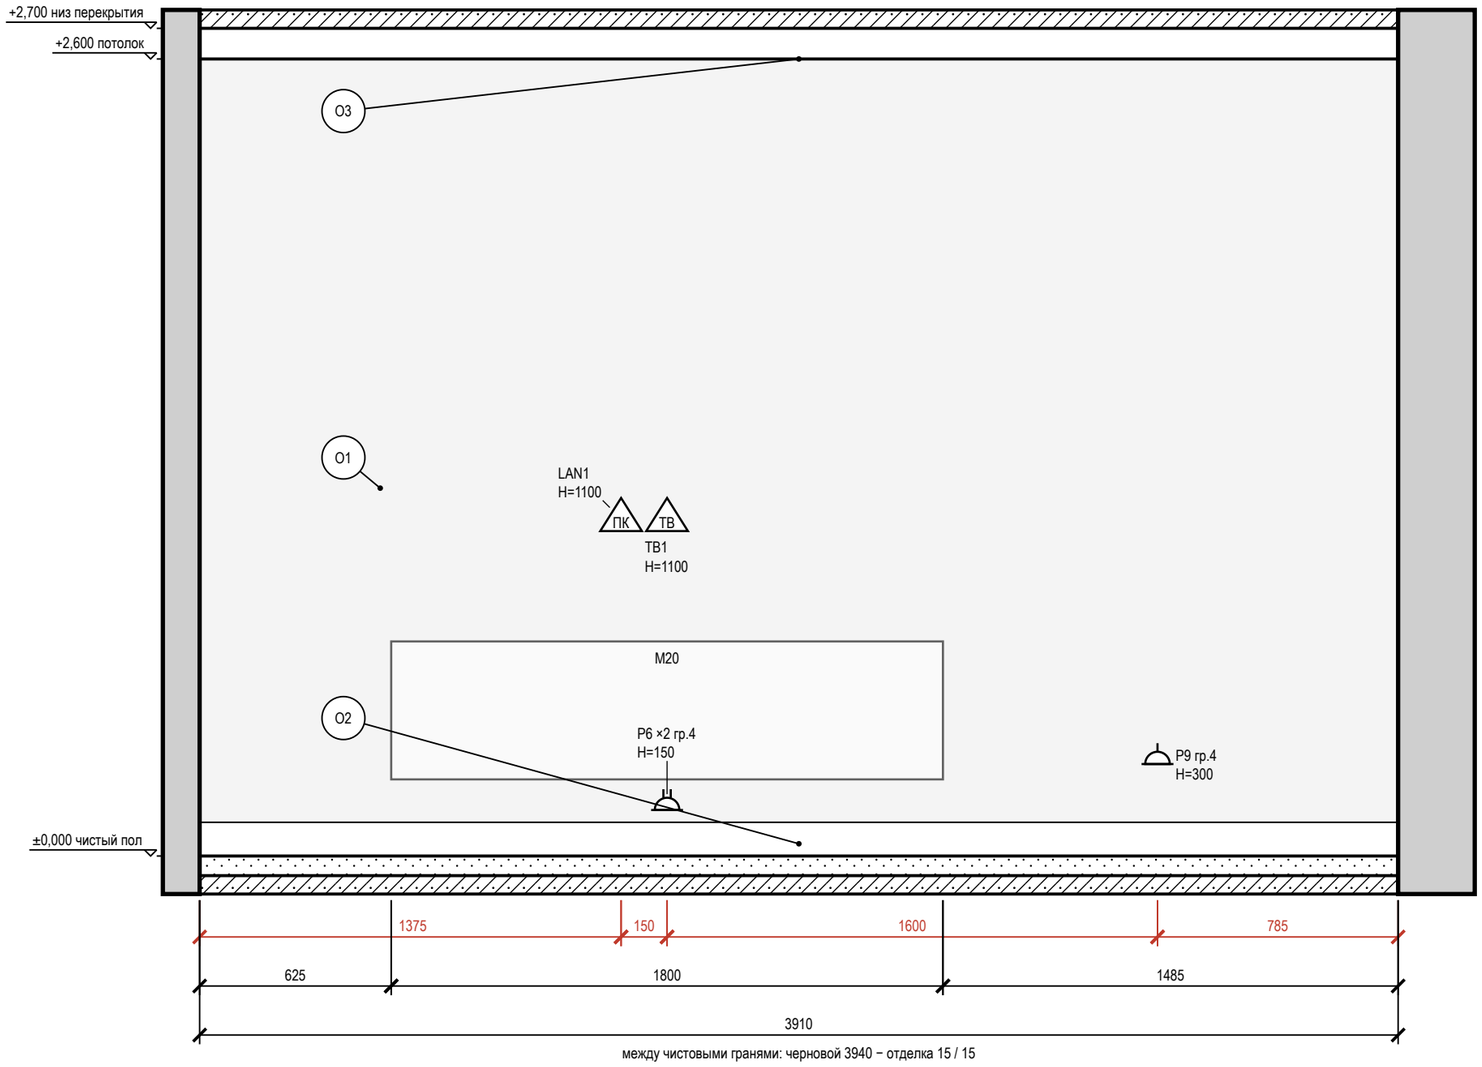


## Схема развёрток (М 1:100)

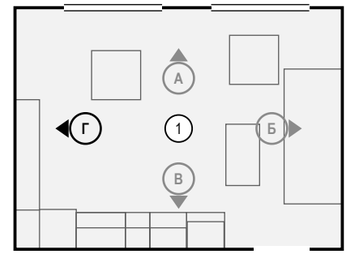


## Условные обозначения

- розетка с заземляющим контактом; у знака — марка, ×N постов в рамке, гр. — группа щита, Н — высота оси, мм
- ПК — розетка компьютерная RJ45
- ТВ — розетка телевизионная
- привязки точек и выводов от угла и от пола, мм
- мебель и приборы — фасад по расстановке (условно)
- стены и перекрытия в сечении
- О1 — марка отделки по реестру отделки альбома
- А — марка развёртки: буква стены, стрелка — взгляд

## Ведомость отделки (на листе)

| Марка | Поверхность | Материал, изделие | Цвет, код | Кол. |
|---|---|---|---|---|
| О1 | стены | окраска, Tikkurila, шелковисто-матовая, подготовка Q3 | NCS S 1002-Y50R | 10,2 м² |
| О2 | плинтус | плинтус МДФ, Orac Decor Luxxus, h 110 мм, SX184, шелковисто-матовая | NCS S 0300-N | 3,9 м |
| О3 | потолок | окраска, Tikkurila, глубокоматовая | NCS S 0300-N | 21 м² |

**Допущения и предложения на листе**

Основа листа: размеры сняты с плана заказчика, контрольный обмер не выполнен (К-5); высота потолка 2700 мм принята: на плане заказчика не указана (К-5); подрайон климата не задан — принят не северный (жилые от 2,5 м) (К-4); толщины стен приняты: наружные 250 мм, перегородки 120 мм — не обмерены (К-5); разрешённая мощность 15 кВт принята по типовой квартире, технических условий нет (К-6).

См. лист открытых вопросов (лист 6, записи К-4–К-6).

## Примечания

1. Развёртки — вид на стену изнутри помещения, по часовой стрелке; расположение — на схеме листа и на листе 60; размеры — в мм по чистовым поверхностям; отметки — в м от ±0,000; высоты Н — от чистого пола помещения до оси изделия, у декора — до центра.
2. Красная цепочка — привязки электроточек и выводов по осям от угла чистовых стен; высота Н — у знака, от чистого пола до оси; высоты мебели, проёмов и границ отделки — колонкой отметок слева. Стена с 5 и более точками или с мелкими звеньями привязок показана двумя видами: архитектурная развёртка (мебель, отделка, проёмы, высоты) и вид «Привязки» на отдельном листе — точки и выводы с марками, одна цепочка по осям и таблица привязок (каждая точка — строка).
3. У знака электроточки: марка (Р — розетка, S — выключатель, Св — светильник, ЭВ — вывод кабеля), ×N — число постов в рамке, гр. — группа щита, Н — высота оси от чистого пола, мм; группы по клавишам выключателя — на листе выключателей.
4. Схема мебели, приборов и декора не является технической документацией для производства мебели; габариты — по паспортам изделий.
5. Потолок — у каждой стены свой, по плану потолков (ПТ2); ступени — зоной, кромка короба перед нишей — тонкой линией; в поле потолка: ПТ1 +2,550.

1000 мм · печать 1:1

| Изм. | Кол.уч | Лист | № док. | Подп. | Дата |
|---|---|---|---|---|---|
| Разраб. | | Кырлан А.С. | | | 04.11.26 |
| Пров. | | | | | |
| ГИП | | | | | |
| | | | | | |
| Н. контр. | | | | | |
| Утв. | | | | | |

**ГД-2026-006-АИ**

Квартира 58 м²

Общая площадь 55,23* м² · * размеры приняты, не замерены (реестр — л. 6, 7, К-5)

Дизайн-проект интерьера

| Стадия | Лист | Листов |
|---|---|---|
| РП | 65 | 87 |

**Развёртка стены Г. Кухня-гостиная (пом. 1)**

М 1:20

**Кырлан Александр Сергеевич**


выпуск 04.11.2026 № 3da8f16a26 · стр. 73 из 96

# Развёртка стены А. Спальня (пом. 2)

Спальня (пом. 2) · вид изнутри помещения · размеры в мм, отметки в м


ПРЕДВАРИТЕЛЬНО · не для производства работ · открыто пунктов: 10 (реестр — л. 6, 7)

## Развёртка стены А

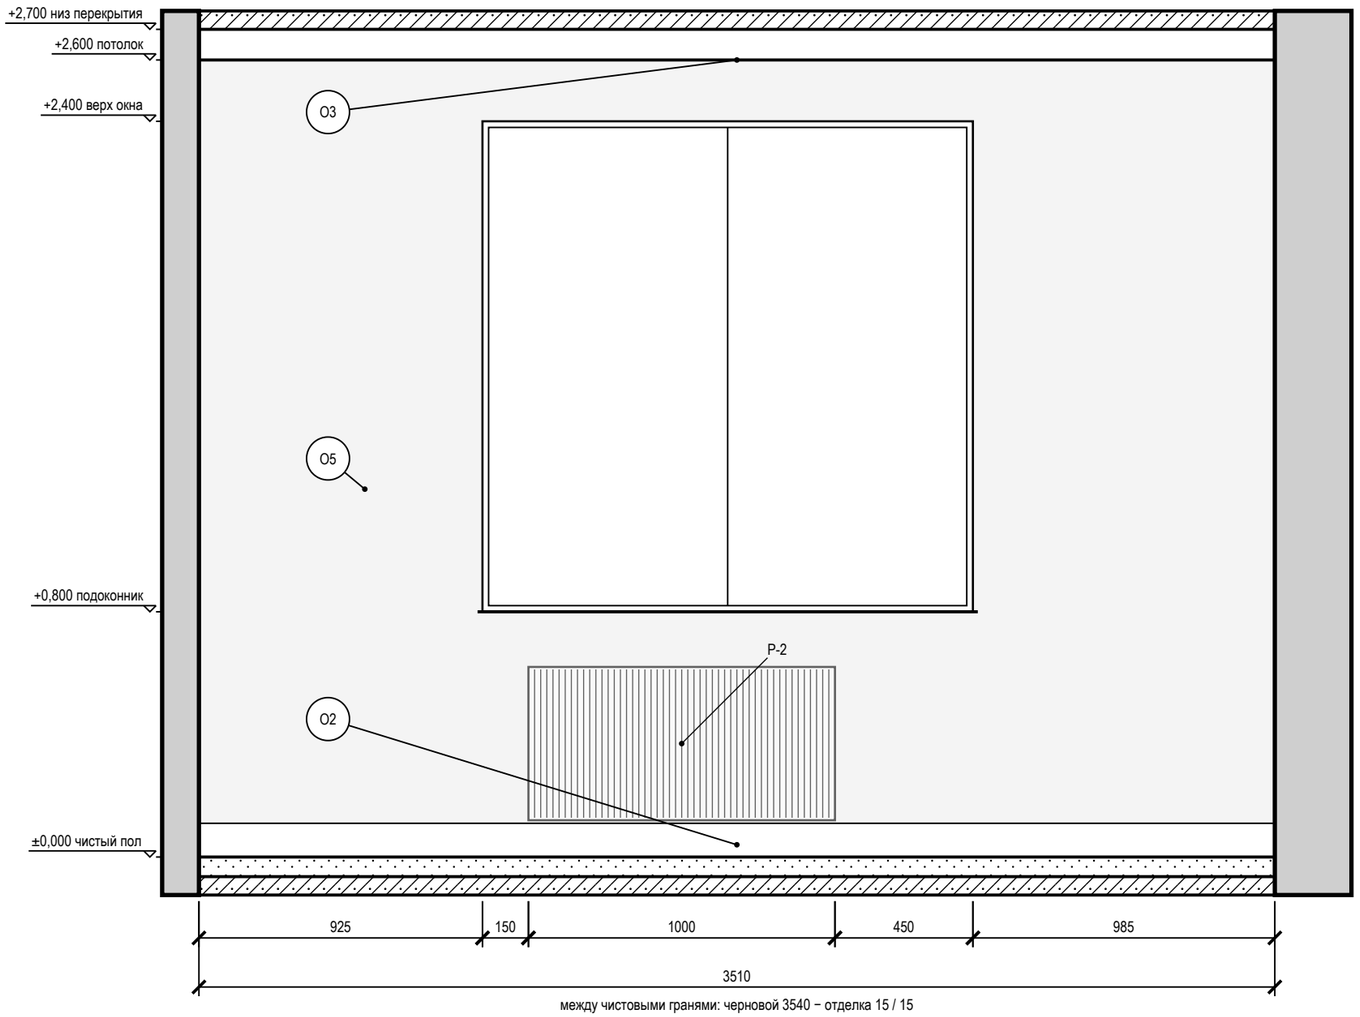


между чистовыми гранями: черновой 3540 − отделка 15 / 15

## Схема развёрток (М 1:100)

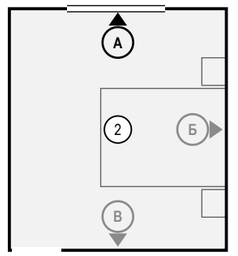


## Условные обозначения

- мебель и приборы — фасад по расстановке (условно)
- окно: проём, рама, подоконник
- радиатор отопления; марка — по плану отопления
- стены и перекрытия в сечении
- О1 — марка отделки по реестру отделки альбома
- А — марка развёртки: буква стены, стрелка — взгляд

## Ведомость отделки (на листе)

| Марка | Поверхность | Материал, изделие | Цвет, код | Кол. |
|---|---|---|---|---|
| О2 | плинтус | плинтус МДФ, Orac Decor Luxxus, h 110 мм, SX184, шелковисто-матовая | NCS S 0300-N | 3,5 м |
| О3 | потолок | окраска, Tikkurila, глубокоматовая | NCS S 0300-N | 13,9 м² |
| О5 | стены | окраска, Tikkurila, глубокоматовая, подготовка Q3 | NCS S 1502-Y50R | 6,6 м² |

## Примечания

1. Развёртки — вид на стену изнутри помещения, по часовой стрелке; расположение — на схеме листа и на листе 60; размеры — в мм по чистовым поверхностям; отметки — в м от ±0,000; высоты Н — от чистого пола помещения до оси изделия, у декора — до центра.
2. Схема мебели, приборов и декора не является технической документацией для производства мебели; габариты — по паспортам изделий.
3. Потолок — у каждой стены свой, по плану потолков (ПТ2); ступени — зоной, кромка короба перед нишей — тонкой линией; в поле потолка: ПТ1 +2,550.

**Допущения и предложения на листе**

Основа листа: размеры сняты с плана заказчика, контрольный обмер не выполнен (К-5); высота потолка 2700 мм принята: на плане заказчика не указана (К-5); подрайон климата не задан — принят не северный (жилые от 2,5 м) (К-4); толщины стен приняты: наружные 250 мм, перегородки 120 мм — не обмерены (К-5); разрешённая мощность 15 кВт принята по типовой квартире, технических условий нет (К-6).

См. лист открытых вопросов (лист 6, записи К-4–К-6).

1000 мм · печать 1:1

| Изм. | Кол.уч | Лист | № док. | Подп. | Дата |
|---|---|---|---|---|---|
| Разраб. | | Кырлан А.С. | | | 04.11.26 |
| Пров. | | | | | |
| ГИП | | | | | |
| | | | | | |
| Н. контр. | | | | | |
| Утв. | | | | | |

**ГД-2026-006-АИ**

Квартира 58 м²

Общая площадь 55,23* м² · * размеры приняты, не замерены (реестр — л. 6, 7, К-5)

Дизайн-проект интерьера

| Стадия | Лист | Листов |
|---|---|---|
| РП | 66 | 87 |

**Развёртка стены А. Спальня (пом. 2)**

М 1:20

**Кырлан Александр Сергеевич**


выпуск 04.11.2026 № 3da8f16a26 · стр. 74 из 96

# Развёртка стены Б. Спальня (пом. 2)

Спальня (пом. 2) · вид изнутри помещения · размеры в мм, отметки в м


ПРЕДВАРИТЕЛЬНО · не для производства работ · открыто пунктов: 10 (реестр — л. 6, 7)

## Развёртка стены Б

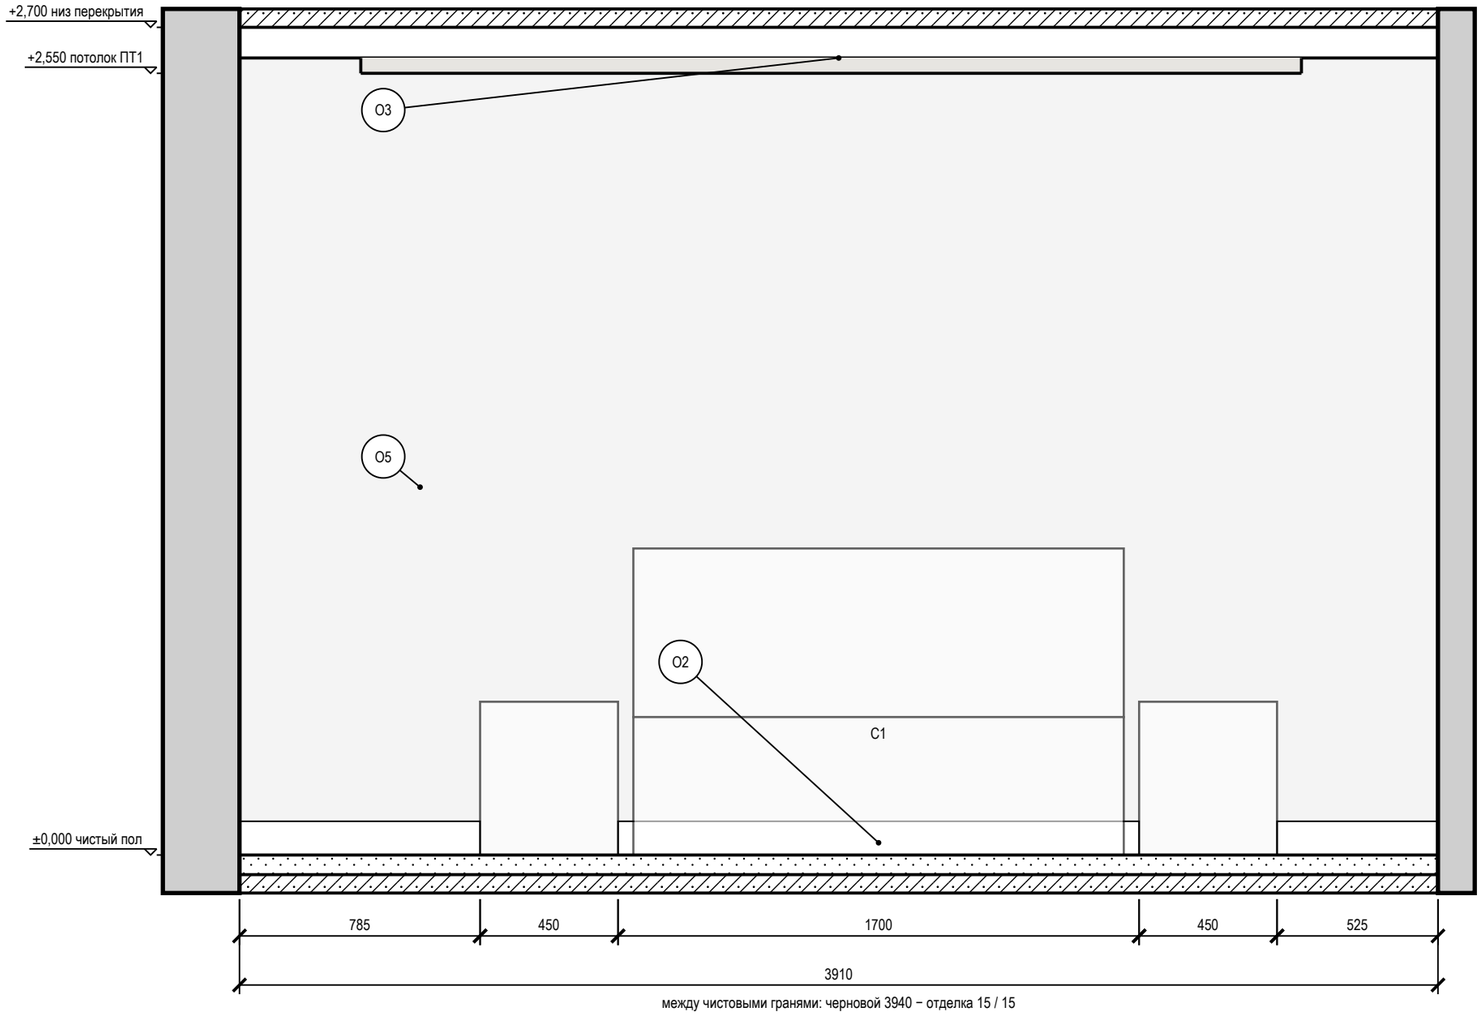


между чистовыми гранями: черновой 3940 − отделка 15 / 15

## Схема развёрток (М 1:100)

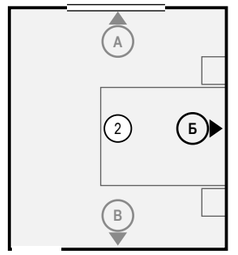


## Условные обозначения

- мебель и приборы — фасад по расстановке (условно)
- стены и перекрытия в сечении
- О1 — марка отделки по реестру отделки альбома
- А — марка развёртки: буква стены, стрелка — взгляд

## Ведомость отделки (на листе)

| Марка | Поверхность | Материал, изделие | Цвет, код | Кол. |
|---|---|---|---|---|
| О2 | плинтус | плинтус МДФ, Orac Decor Luxxus, h 110 мм, SX184, шелковисто-матовая | NCS S 0300-N | 3 м |
| О3 | потолок | окраска, Tikkurila, глубокоматовая | NCS S 0300-N | 13,9 м² |
| О5 | стены | окраска, Tikkurila, глубокоматовая, подготовка Q3 | NCS S 1502-Y50R | 10,2 м² |

## Примечания

1. Развёртки — вид на стену изнутри помещения, по часовой стрелке; расположение — на схеме листа и на листе 60; размеры — в мм по чистовым поверхностям; отметки — в м от ±0,000; высоты Н — от чистого пола помещения до оси изделия, у декора — до центра.
2. Стена Б показана двумя видами: здесь — архитектурная развёртка (мебель, отделка, проёмы, высоты), электроточки и выводы ВК с привязками и таблицей — на листе 68 («Привязки»).
3. Схема мебели, приборов и декора не является технической документацией для производства мебели; габариты — по паспортам изделий.
4. Потолок — у каждой стены свой, по плану потолков (ПТ2, ПТ1); ступени — зоной, кромка короба перед нишей — тонкой линией.

**Допущения и предложения на листе**

Основа листа: размеры сняты с плана заказчика, контрольный обмер не выполнен (К-5); высота потолка 2700 мм принята: на плане заказчика не указана (К-5); подрайон климата не задан — принят не северный (жилые от 2,5 м) (К-4); толщины стен приняты: наружные 250 мм, перегородки 120 мм — не обмерены (К-5); разрешённая мощность 15 кВт принята по типовой квартире, технических условий нет (К-6).

См. лист открытых вопросов (лист 6, записи К-4–К-6).

1000 мм · печать 1:1

| Изм. | Кол.уч | Лист | № док. | Подп. | Дата |
|---|---|---|---|---|---|
| Разраб. | | Кырлан А.С. | | | 04.11.26 |
| Пров. | | | | | |
| ГИП | | | | | |
| | | | | | |
| Н. контр. | | | | | |
| Утв. | | | | | |

**ГД-2026-006-АИ**

Квартира 58 м²

Общая площадь 55,23* м² · * размеры приняты, не замерены (реестр — л. 6, 7, К-5)

Дизайн-проект интерьера

| Стадия | Лист | Листов |
|---|---|---|
| РП | 67 | 87 |

**Развёртка стены Б. Спальня (пом. 2)**

М 1:20


**Кырлан Александр Сергеевич**

# Привязки электроточек, стена Б. Спальня (пом. 2)

Спальня (пом. 2) · вид изнутри помещения · привязки в мм, отметки в м · к развёртке на листе 67

ПРЕДВАРИТЕЛЬНО · не для производства работ · открыто пунктов: 10 (реестр — л. 6, 7)

## Развёртка стены Б: электроточки и выводы

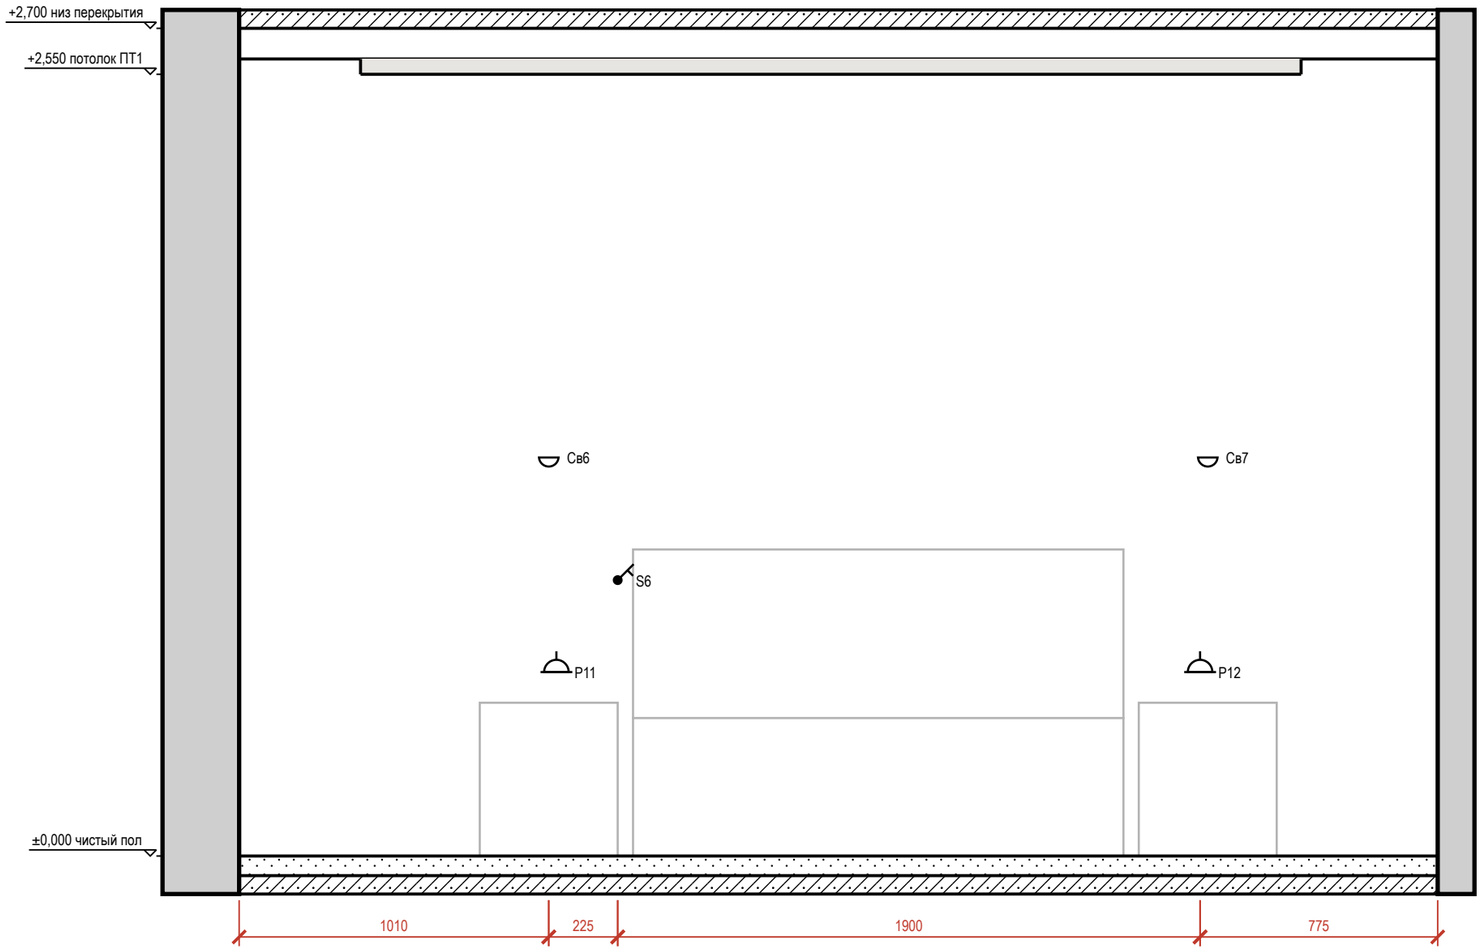



## Таблица привязок электроточек и выводов

| Марка | Назначение | От угла, мм | Н от пола, мм | Примечание |
|---|---|---|---|---|
| Св6 | светильник настенный | 1010 | 1300 | гр. 1 |
| Р11 | розетка | 1035 | 600 | гр. 4 |
| S6 | выключатель | 1235 | 900 | гр. 1 |
| Р12 | розетка | 3135 | 600 | гр. 4 |
| Св7 | светильник настенный | 3160 | 1300 | гр. 1 |

## Условные обозначения

- розетка с заземляющим контактом; у знака — марка, ×N постов в рамке, гр. — группа щита, Н — высота оси, мм
- выключатель одноклавишный
- светильник настенный (бра), Н — высота оси
- привязки точек и выводов от угла и от пола, мм
- марка развёртки: буква стены, стрелка — взгляд

## Схема развёрток (М 1:50)

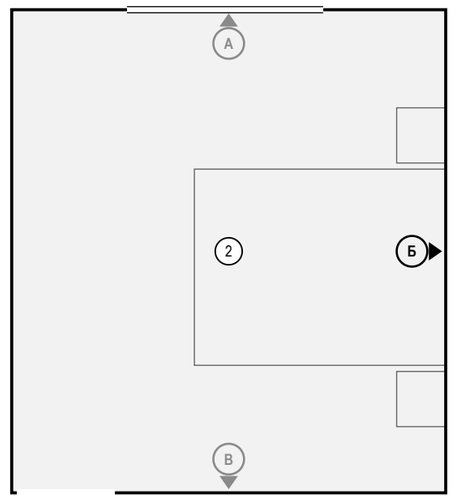


## Примечания

1. Вид «Привязки» стены Б — электроточки и выводы ВК; архитектурная развёртка (мебель, отделка, проёмы, высоты) — на листе 67, расположение — на листе 60. Мебель и приборы — подложкой для ориентира; их марки и обозначения мебели, проёмов и стен — там же.
2. Привязки — в мм: по горизонтали от левого чистового угла стены до оси изделия, Н — от чистого пола до оси; все точки — в таблице привязок. Красная цепочка — привязки по осям; точки ближе 120 мм одна к другой в цепочку не дробятся — их привязки только в таблице.
3. У знака — марка электроточки (Р — розетка, S — выключатель, Св — светильник, ЭВ — вывод кабеля); посты в рамке и группа щита — в графе «Примечание»; группы по клавишам выключателя — на листе выключателей.

**Допущения и предложения на листе**

Основа листа: размеры сняты с плана заказчика, контрольный обмер не выполнен (К-5); высота потолка 2700 мм принята: на плане заказчика не указана (К-5); подрайон климата не задан — принят не северный (жилые от 2,5 м) (К-4); толщины стен приняты: наружные 250 мм, перегородки 120 мм — не обмерены (К-5); разрешённая мощность 15 кВт принята по типовой квартире, технических условий нет (К-6).

См. лист открытых вопросов (лист 6, записи К-4–К-6).

1000 мм · печать 1:1

| Изм. | Кол.уч | Лист | № док. | Подп. | Дата |
|---|---|---|---|---|---|
| Разраб. | | Кырлан А.С. | | | 04.11.26 |
| Пров. | | | | | |
| ГИП | | | | | |
| | | | | | |
| Н. контр. | | | | | |
| Утв. | | | | | |

**ГД-2026-006-АИ**

Квартира 58 м²

Общая площадь 55,23* м² · * размеры приняты, не замерены (реестр — л. 6, 7, К-5)

Дизайн-проект интерьера

| Стадия | Лист | Листов |
|---|---|---|
| РП | 68 | 87 |

**Привязки электроточек, стена Б. Спальня (пом. 2)**

М 1:20

**Кырлан Александр Сергеевич**


выпуск 04.11.2026 № 3da8f16a26 · стр. 76 из 96

# Развёртка стены В. Спальня (пом. 2)


Спальня (пом. 2) · вид изнутри помещения · размеры в мм, отметки в м

ПРЕДВАРИТЕЛЬНО · не для производства работ · открыто пунктов: 10 (реестр — л. 6, 7)

## Развёртка стены В

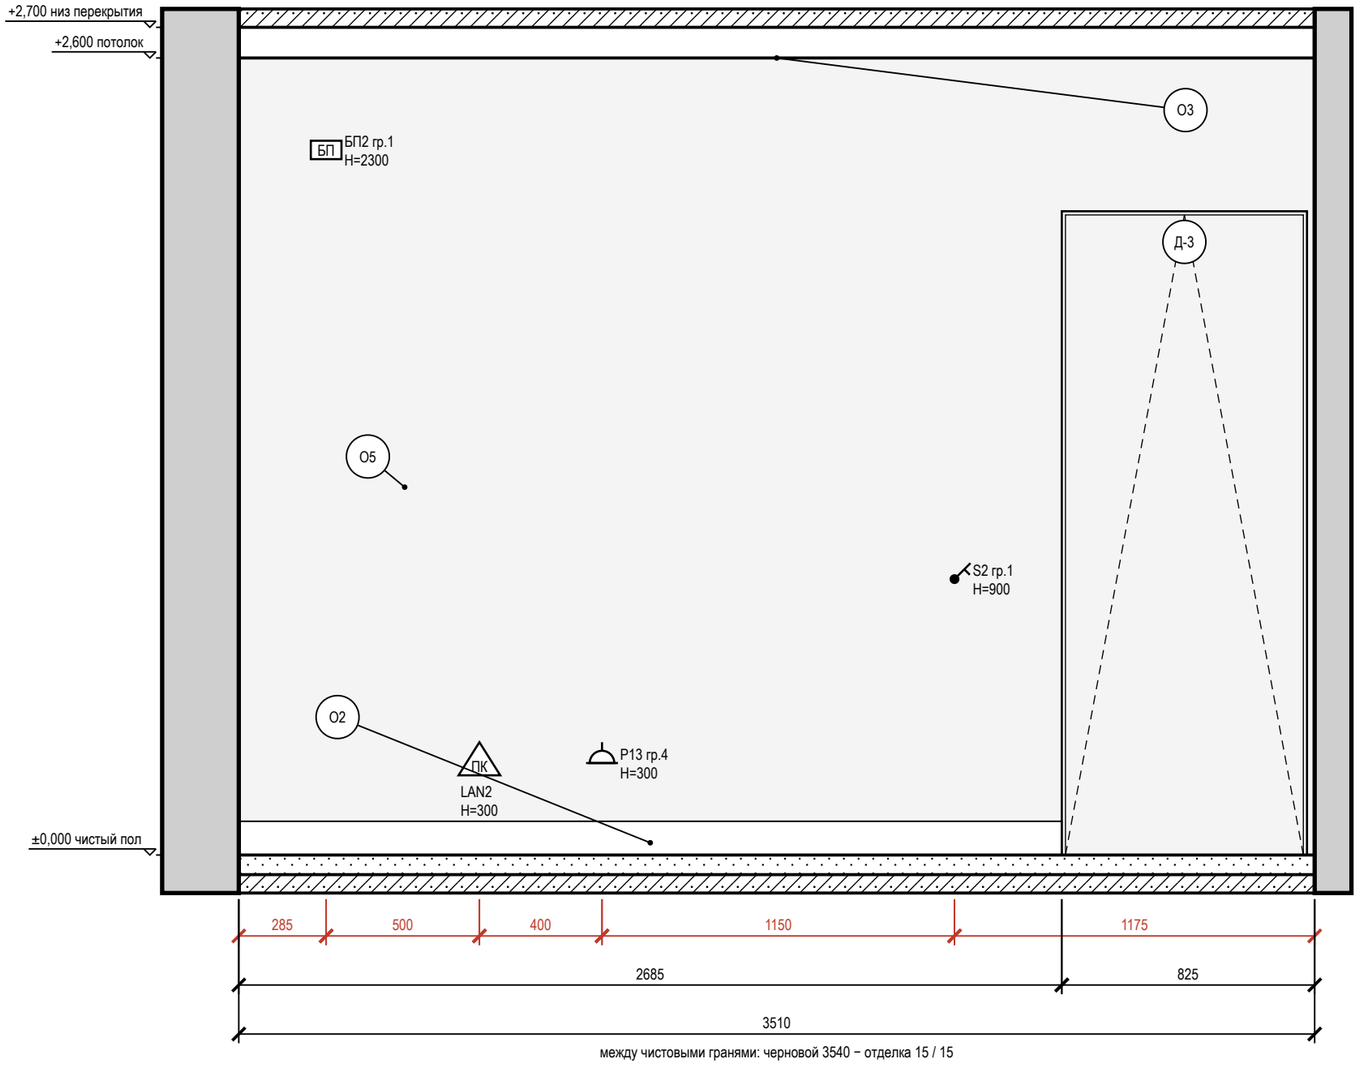


## Схема развёрток (М 1:100)

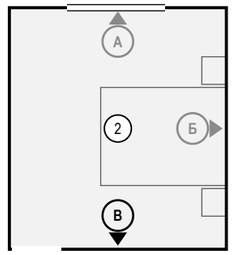


## Условные обозначения

- розетка с заземляющим контактом; у знака — марка, ×N постов в рамке, гр. — группа щита, Н — высота оси, мм
- выключатель одноклавишный
- БП — блок питания LED, с доступом (люк от 100×100 мм)
- ПК — розетка компьютерная RJ45
- привязки точек и выводов от угла и от пола, мм
- мебель и приборы — фасад по расстановке (условно)
- дверь скрытого монтажа: полотно в плоскости стены (узел — на листе узлов)
- стены и перекрытия в сечении
- О1 — марка отделки по реестру отделки альбома
- А — марка развёртки: буква стены, стрелка — взгляд

## Ведомость отделки (на листе)

| Марка | Поверхность | Материал, изделие | Цвет, код | Кол. |
|---|---|---|---|---|
| О2 | плинтус | плинтус МДФ, Orac Decor Luxxus, h 110 мм, SX184, шелковисто-матовая | NCS S 0300-N | 2,7 м |
| О3 | потолок | окраска, Tikkurila, глубокоматовая | NCS S 0300-N | 13,9 м² |
| О5 | стены | окраска, Tikkurila, глубокоматовая, подготовка Q3 | NCS S 1502-Y50R | 7,4 м² |

**Допущения и предложения на листе**

Основа листа: размеры сняты с плана заказчика, контрольный обмер не выполнен (К-5); высота потолка 2700 мм принята: на плане заказчика не указана (К-5); подрайон климата не задан — принят не северный (жилые от 2,5 м) (К-4); толщины стен приняты: наружные 250 мм, перегородки 120 мм — не обмерены (К-5); разрешённая мощность 15 кВт принята по типовой квартире, технических условий нет (К-6).

См. лист открытых вопросов (лист 6, записи К-4–К-6).

## Примечания

1. Развёртки — вид на стену изнутри помещения, по часовой стрелке; расположение — на схеме листа и на листе 60; размеры — в мм по чистовым поверхностям; отметки — в м от ±0,000; высоты Н — от чистого пола помещения до оси изделия, у декора — до центра.
2. Красная цепочка — привязки электроточек и выводов по осям от угла чистовых стен; высота Н — у знака, от чистого пола до оси; высоты мебели, проёмов и границ отделки — колонкой отметок слева. Стена с 5 и более точками или с мелкими звеньями привязок показана двумя видами: архитектурная развёртка (мебель, отделка, проёмы, высоты) и вид «Привязки» на отдельном листе — точки и выводы с марками, одна цепочка по осям и таблица привязок (каждая точка — строка).
3. У знака электроточки: марка (Р — розетка, S — выключатель, Св — светильник, ЭВ — вывод кабеля), ×N — число постов в рамке, гр. — группа щита, Н — высота оси от чистого пола, мм; группы по клавишам выключателя — на листе выключателей.
4. Схема мебели, приборов и декора не является технической документацией для производства мебели; габариты — по паспортам изделий.
5. Двери скрытого монтажа — полотно в плоскости стены, отделка стены по полотну, плинтус прерывается у короба (узел — на листе узлов).
6. Потолок — у каждой стены свой, по плану потолков (ПТ2); ступени — зоной, кромка короба перед нишей — тонкой линией; в поле потолка: ПТ1 +2,550.

1000 мм · печать 1:1

| Изм. | Кол.уч | Лист | № док. | Подп. | Дата |
|---|---|---|---|---|---|
| Разраб. | | Кырлан А.С. | | | 04.11.26 |
| Пров. | | | | | |
| ГИП | | | | | |
| Н. контр. | | | | | |
| Утв. | | | | | |

**ГД-2026-006-АИ**

Квартира 58 м²

Общая площадь 55,23* м² · * размеры приняты, не замерены (реестр — л. 6, 7, К-5)

Дизайн-проект интерьера

| Стадия | Лист | Листов |
|---|---|---|
| РП | 69 | 87 |

**Развёртка стены В. Спальня (пом. 2)**

М 1:20

**Кырлан Александр Сергеевич**


выпуск 04.11.2026 № 3da8f16a26 · стр. 77 из 96

# Развёртки стен А, Б, В. Ванная (пом. 3)

Ванная (пом. 3) · вид изнутри помещения · размеры в мм, отметки в м


ПРЕДВАРИТЕЛЬНО · не для производства работ · открыто пунктов: 10 (реестр — л. 6, 7)

## Развёртка стены А

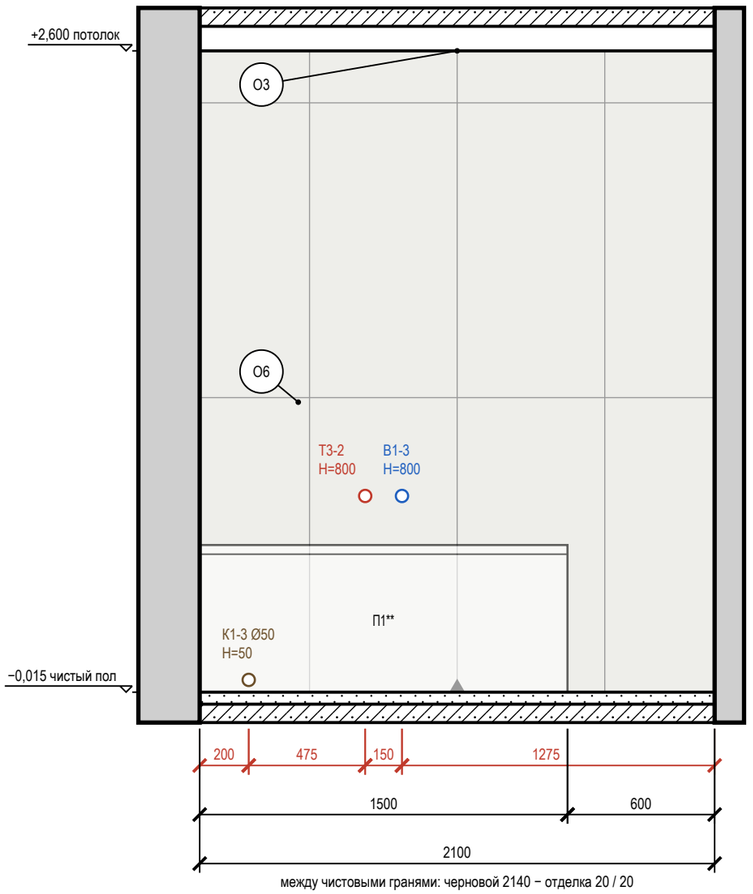



между чистовыми гранями: черновой 2140 − отделка 20 / 20

## Развёртка стены Б

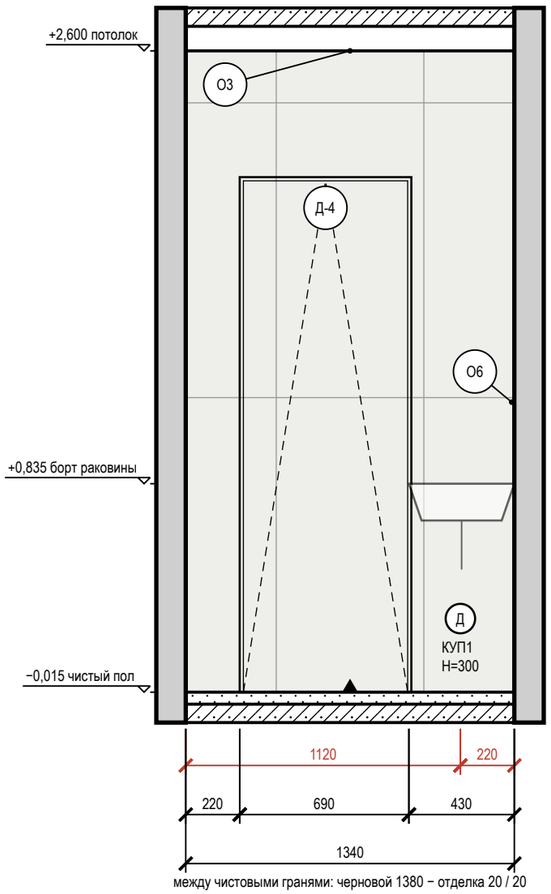



между чистовыми гранями: черновой 1380 − отделка 20 / 20

## Развёртка стены В

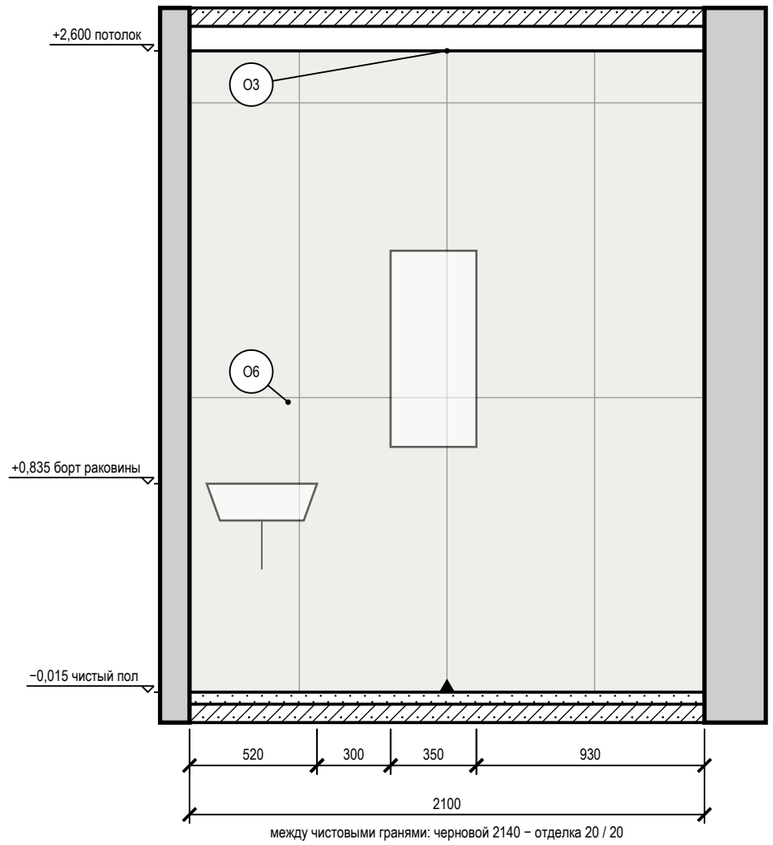


между чистовыми гранями: черновой 2140 − отделка 20 / 20

## Схема развёрток (М 1:100)

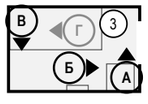


## Условные обозначения

- вывод В1 (код — в ведомости привязок)
- вывод Т3 (код — в ведомости привязок)
- вывод К1 (код — в ведомости привязок)
- привязки точек и выводов от угла и от пола, мм
- мебель и приборы — фасад по расстановке (условно)
- дверь скрытого монтажа: полотно в плоскости стены (узел — на листе узлов)
- стены и перекрытия в сечении
- плитка: сетка швов по формату, ▲ — ось старта
- О1 — марка отделки по реестру отделки альбома
- А — марка развёртки: буква стены, стрелка — взгляд

## Ведомость отделки (на листе)

| Марка | Поверхность | Материал, изделие | Цвет, код | Кол. |
|---|---|---|---|---|
| О3 | потолок | окраска, Tikkurila, глубокоматовая | NCS S 0300-N | 3 м² |
| О6 | стены | облицовка плиткой, Italon Charme Extra, 600×1200 мм, 610015000370 | Italon 610015000370 «Charme Extra» | 13 м² |

Допущения и предложения на листе. Знак «**» предложено (согласовать). См. лист открытых вопросов (листы 6, 7).

## Примечания

1. Развёртки — вид на стену изнутри помещения, по часовой стрелке; расположение — на схеме листа и на листе 60; размеры — в мм по чистовым поверхностям; отметки — в м от ±0,000; высоты Н — от чистого пола помещения до оси изделия, у декора — до центра.
2. Красная цепочка — привязки электроточек и выводов по осям от угла чистовых стен; высота Н — у знака, от чистого пола до оси; высоты мебели, проёмов и границ отделки — колонкой отметок слева. Стена с 5 и более точками или с мелкими звеньями привязок показана двумя видами: архитектурная развёртка (мебель, отделка, проёмы, высоты) и вид «Привязки» на отдельном листе — точки и выводы с марками, одна цепочка по осям и таблица привязок (каждая точка — строка).
3. Стена В показана двумя видами: здесь — архитектурная развёртка (мебель, отделка, проёмы, высоты), электроточки и выводы ВК с привязками и таблицей — на листе 71 («Привязки»).
4. У знака электроточки: марка (Р — розетка, S — выключатель, Св — светильник, ЭВ — вывод кабеля), ×N — число постов в рамке, гр. — группа щита, Н — высота оси от чистого пола, мм; группы по клавишам выключателя — на листе выключателей.
5. Схема мебели, приборов и декора не является технической документацией для производства мебели; габариты — по паспортам изделий.
6. Облицовка — по сетке швов, раскладка от оси стены (треугольник у пола); подрезки — по листу раскладки плитки.
7. Гидроизоляция в 2 слоя, заход на стены 200 мм; над ванной — до 2000 и 300 мм за борт — до облицовки, с актом скрытых работ и тестом проливом (узел — на листе узлов).
8. Двери скрытого монтажа — полотно в плоскости стены, отделка стены по полотну, плинтус прерывается у короба (узел — на листе узлов).

1000 мм · печать 1:1

| | | | | | |
|---|---|---|---|---|---|
| | | | | | |
| | | | | | |
| | | | | | |
| Изм. | Кол.уч | Лист | № док. | Подп. | Дата |
| Разраб. | | Кырлан А.С. | | | 04.11.26 |
| Пров. | | | | | |
| ГИП | | | | | |
| | | | | | |
| Н. контр. | | | | | |
| Утв. | | | | | |

**ГД-2026-006-АИ**

Квартира 58 м²

Общая площадь 55,23* м² · * размеры приняты, не замерены (реестр — л. 6, 7, К-5)

Дизайн-проект интерьера

| Стадия | Лист | Листов |
|---|---|---|
| РП | 70 | 87 |

**Развёртки стен А, Б, В. Ванная (пом. 3)**

М 1:25

**Кырлан Александр Сергеевич**


выпуск 04.11.2026 № 3da8f16a26 · стр. 78 из 96

# Привязки электроточек и выводов ВК, стена В. Ванная (пом. 3)

Ванная (пом. 3) · вид изнутри помещения · привязки в мм, отметки в м · к развёртке на листе 70

ПРЕДВАРИТЕЛЬНО · не для производства работ · открыто пунктов: 10 (реестр — л. 6, 7)

## Развёртка стены В: электроточки и выводы

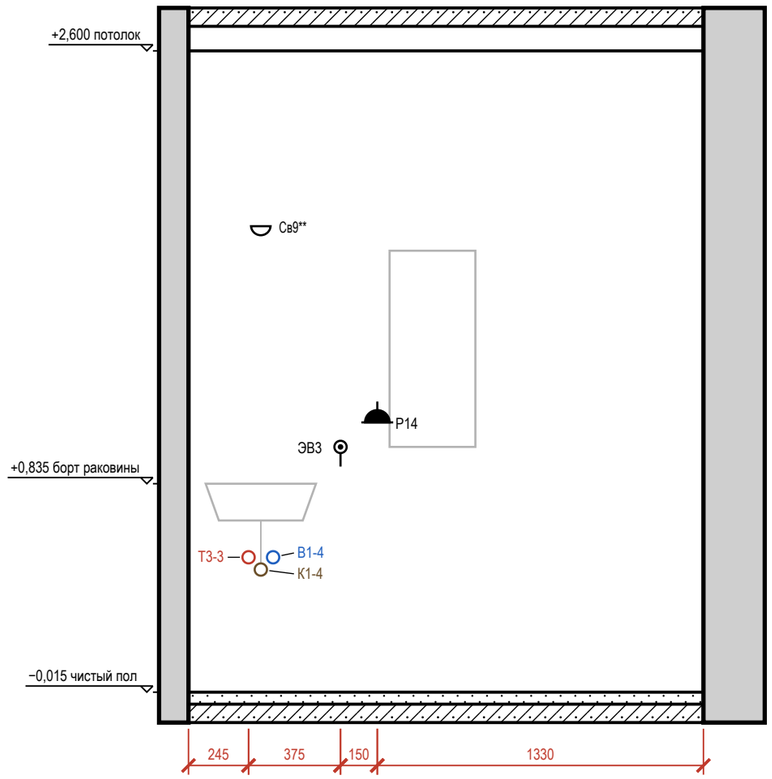



## Таблица привязок электроточек и выводов

| Марка | Назначение | От угла, мм | Н от пола, мм | Примечание |
|---|---|---|---|---|
| Т3-3 | горячая вода — умывальник | 245 | 550 | межос. 100 |
| К1-4 | канализация — умывальник | 295 | 500 | Ø50 |
| Св9** | светильник настенный | 295 | 1900 | гр. 1 |
| В1-4 | холодная вода — умывальник | 345 | 550 | межос. 100 |
| ЭВ3 | вывод кабеля: полотенцесушитель | 620 | 1000 | гр. 5 |
| Р14 | розетка: фен | 770 | 1100 | гр. 5, IP44 |

## Условные обозначения

- розетка влагозащищённая IP44
- вывод кабеля для подключения прибора (без розетки), марка ЭВ
- светильник настенный (бра), Н — высота оси
- вывод В1 (код — в ведомости привязок)
- вывод Т3 (код — в ведомости привязок)
- вывод К1 (код — в ведомости привязок)
- привязки точек и выводов от угла и от пола, мм
- марка развёртки: буква стены, стрелка — взгляд

## Схема развёрток (М 1:50)

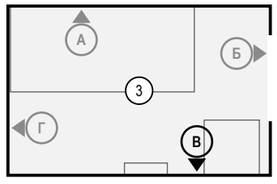


## Примечания

1. Вид «Привязки» стены В — электроточки и выводы ВК; архитектурная развёртка (мебель, отделка, проёмы, высоты) — на листе 70, расположение — на листе 60. Мебель и приборы — подложкой для ориентира; их марки и обозначения мебели, проёмов и стен — там же.
2. Привязки — в мм: по горизонтали от левого чистового угла стены до оси изделия, Н — от чистого пола до оси; все точки — в таблице привязок. Красная цепочка — привязки по осям; точки ближе 150 мм одна к другой в цепочку не дробятся — их привязки только в таблице.
3. У знака — марка электроточки (Р — розетка, S — выключатель, Св — светильник, ЭВ — вывод кабеля); посты в рамке и группа щита — в графе «Примечание»; группы по клавишам выключателя — на листе выключателей.
4. Коды выводов ВК: В1 — холодная вода, Т3 — горячая вода, К1 — канализация; номер после дефиса — номер вывода на листе выводов сантехники.

**Допущения и предложения на листе**

Основа листа: размеры сняты с плана заказчика, контрольный обмер не выполнен (К-5); высота потолка 2700 мм принята: на плане заказчика не указана (К-5); подрайон климата не задан — принят не северный (жилые от 2,5 м) (К-4); толщины стен приняты: наружные 250 мм, перегородки 120 мм — не обмерены (К-5); разрешённая мощность 15 кВт принята по типовой квартире, технических условий нет (К-6).

Знак «**» — предложение проектировщика, заказчиком не утверждено (согласовать с заказчиком): Св9 — свет у зеркала — над зеркалом у умывальника по его оси (свет на лицо, а не над сантехникой).

См. лист открытых вопросов (лист 6, записи К-4–К-6).

1000 мм · печать 1:1

| Изм. | Кол.уч | Лист | № док. | Подп. | Дата |
|---|---|---|---|---|---|
| Разраб. | | Кырлан А.С. | | | 04.11.26 |
| Пров. | | | | | |
| ГИП | | | | | |
| | | | | | |
| Н. контр. | | | | | |
| Утв. | | | | | |

**ГД-2026-006-АИ**

Квартира 58 м²

Общая площадь 55,23* м² · * размеры приняты, не замерены (реестр — л. 6, 7, К-5)

Дизайн-проект интерьера

| Стадия | Лист | Листов |
|---|---|---|
| РП | 71 | 87 |

**Привязки электроточек и выводов ВК, стена В. Ванная (пом. 3)**

М 1:25

**Кырлан Александр Сергеевич**


выпуск 04.11.2026 № 3da8f16a26 · стр. 79 из 96

# Развёртка стены Г. Ванная (пом. 3)

Ванная (пом. 3) · вид изнутри помещения · размеры в мм, отметки в м


ПРЕДВАРИТЕЛЬНО · не для производства работ · открыто пунктов: 10 (реестр — л. 6, 7)

## Развёртка стены Г

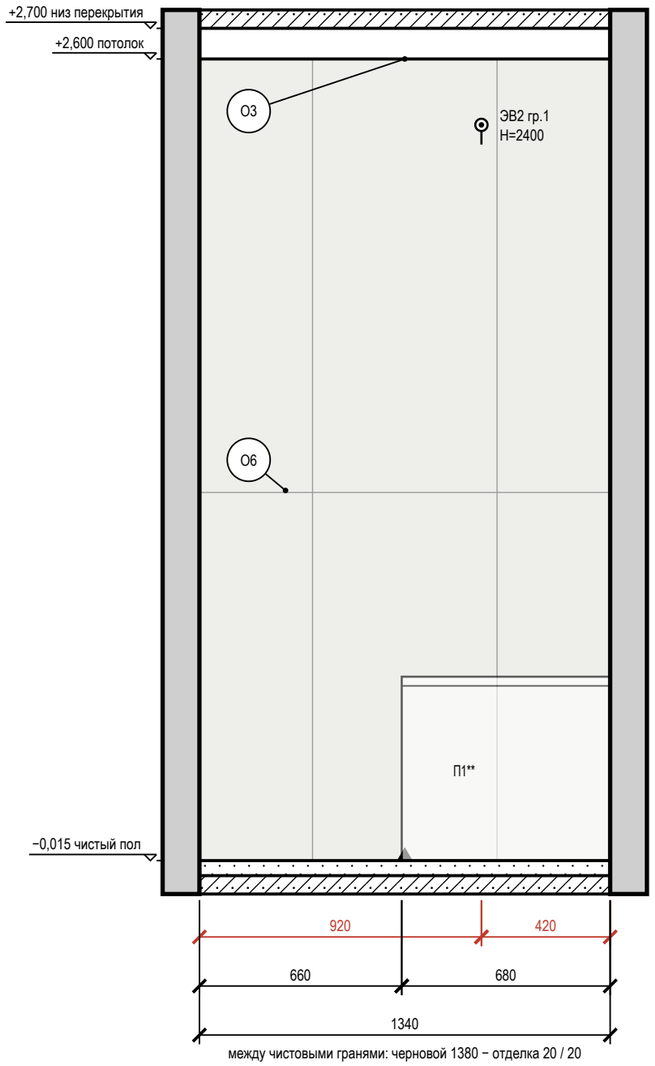


между чистовыми гранями: черновой 1380 − отделка 20 / 20

## Схема развёрток (М 1:100)

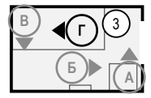


## Условные обозначения

- вывод кабеля для подключения прибора (без розетки), марка ЭВ
- привязки точек и выводов от угла и от пола, мм
- мебель и приборы — фасад по расстановке (условно)
- стены и перекрытия в сечении
- плитка: сетка швов по формату, ▲ — ось старта
- О1 — марка отделки по реестру отделки альбома
- А — марка развёртки: буква стены, стрелка — взгляд

## Ведомость отделки (на листе)

| Марка | Поверхность | Материал, изделие | Цвет, код | Кол. |
|---|---|---|---|---|
| О3 | потолок | окраска, Tikkurila, глубокоматовая | NCS S 0300-N | 3 м² |
| О6 | стены | облицовка плиткой, Italon Charme Extra, 600×1200 мм, 610015000370 | Italon 610015000370 «Charme Extra» | 3,5 м² |

**Допущения и предложения на листе**

Основа листа: размеры сняты с плана заказчика, контрольный обмер не выполнен (К-5); высота потолка 2700 мм принята: на плане заказчика не указана (К-5); подрайон климата не задан — принят не северный (жилые от 2,5 м) (К-4); толщины стен приняты: наружные 250 мм, перегородки 120 мм — не обмерены (К-5); разрешённая мощность 15 кВт принята по типовой квартире, технических условий нет (К-6).

Знак «**» — предложение проектировщика, заказчиком не утверждено (согласовать с заказчиком): К-2: П1 — ванна 1500 вместо 1600 — не заходит в проход перед проёмом Д-4; перед ванной 680 мм — глубина помещения.

См. лист открытых вопросов (лист 6, записи К-2, К-4–К-6).

## Примечания

1. Развёртки — вид на стену изнутри помещения, по часовой стрелке; расположение — на схеме листа и на листе 60; размеры — в мм по чистовым поверхностям; отметки — в м от ±0,000; высоты H — от чистого пола помещения до оси изделия, у декора — до центра.
2. Красная цепочка — привязки электроточек и выводов по осям от угла чистовых стен; высота H — у знака, от чистого пола до оси; высоты мебели, проёмов и границ отделки — колонкой отметок слева. Стена с 5 и более точками или с мелкими звеньями привязок показана двумя видами: архитектурная развёртка (мебель, отделка, проёмы, высоты) и вид «Привязки» на отдельном листе — точки и выводы с марками, одна цепочка по осям и таблица привязок (каждая точка — строка).
3. У знака электроточки: марка (Р — розетка, S — выключатель, Св — светильник, ЭВ — вывод кабеля), ×N — число постов в рамке, гр. — группа щита, H — высота оси от чистого пола, мм; группы по клавишам выключателя — на листе выключателей.
4. Схема мебели, приборов и декора не является технической документацией для производства мебели; габариты — по паспортам изделий.
5. Облицовка — по сетке швов, раскладка от оси стены (треугольник у пола); подрезки — по листу раскладки плитки.
6. Гидроизоляция в 2 слоя, заход на стены 200 мм; над ванной — до 2000 и 300 мм за борт — до облицовки, с актом скрытых работ и тестом проливом (узел — на листе узлов).

1000 мм · печать 1:1

| Изм. | Кол.уч | Лист | № док. | Подп. | Дата |
|---|---|---|---|---|---|
| Разраб. | | Кырлан А.С. | | | 04.11.26 |
| Пров. | | | | | |
| ГИП | | | | | |
| | | | | | |
| Н. контр. | | | | | |
| Утв. | | | | | |

**ГД-2026-006-АИ**

Квартира 58 м²

Общая площадь 55,23* м² · * размеры приняты, не замерены (реестр — л. 6, 7, К-5)

Дизайн-проект интерьера

| Стадия | Лист | Листов |
|---|---|---|
| РП | 72 | 87 |

**Развёртка стены Г. Ванная (пом. 3)**

М 1:20

**Кырлан Александр Сергеевич**


выпуск 04.11.2026 № 3da8f16a26 · стр. 80 из 96

# Развёртки стен А, Б, В. Санузел (пом. 4)

Санузел (пом. 4) · вид изнутри помещения · размеры в мм, отметки в м


ПРЕДВАРИТЕЛЬНО · не для производства работ · открыто пунктов: 10 (реестр — л. 6, 7)

### Развёртка стены А

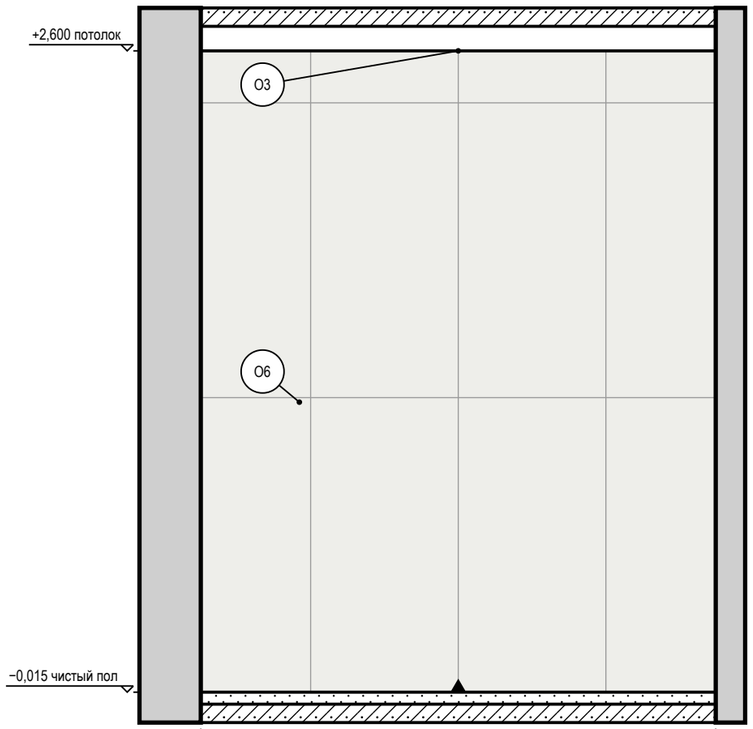



между чистовыми гранями: черновой 2140 − отделка 20 / 20

### Развёртка стены Б

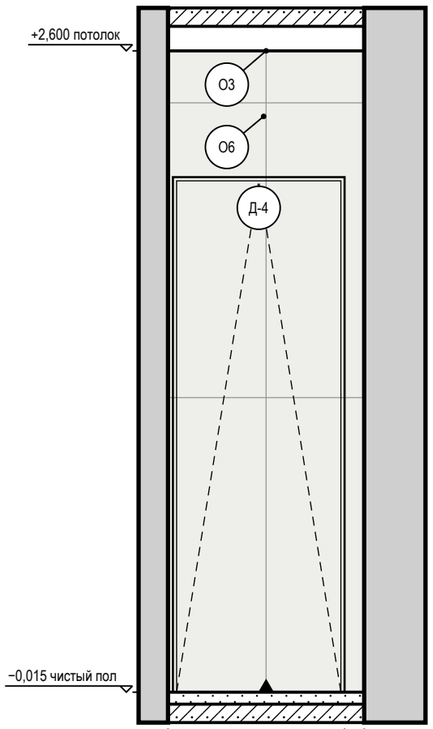



между чистовыми гранями: черновой 840 − отделка 20 / 20

### Развёртка стены В

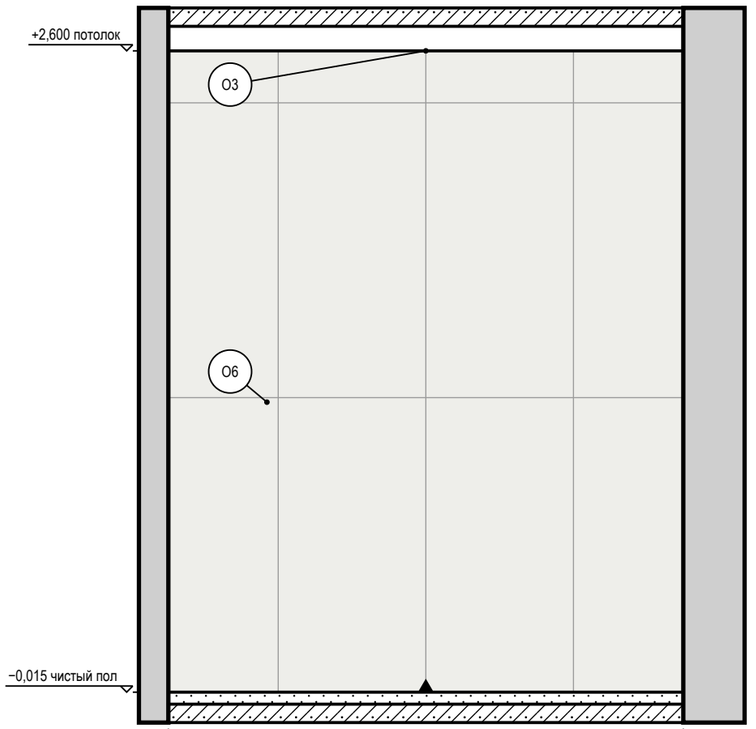


между чистовыми гранями: черновой 2140 − отделка 20 / 20

## Схема развёрток (М 1:100)

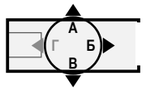


## Условные обозначения

- мебель и приборы — фасад по расстановке (условно)
- дверь скрытого монтажа: полотно в плоскости стены (узел — на листе узлов)
- стены и перекрытия в сечении
- плитка: сетка швов по формату, ▲ — ось старта
- О1 — марка отделки по реестру отделки альбома
- А — марка развёртки: буква стены, стрелка — взгляд

## Ведомость отделки (на листе)

| Марка | Поверхность | Материал, изделие | Цвет, код | Кол. |
|---|---|---|---|---|
| О3 | потолок | окраска, Tikkurila, глубокоматовая | NCS S 0300-N | 1,8 м² |
| О6 | стены | облицовка плиткой, Italon Charme Extra, 600×1200 мм, 610015000370 | Italon 610015000370 «Charme Extra» | 11,6 м² |

## Примечания

1. Развёртки — вид на стену изнутри помещения, по часовой стрелке; расположение — на схеме листа и на листе 60; размеры — в мм по чистовым поверхностям; отметки — в м от ±0,000; высоты Н — от чистого пола помещения до оси изделия, у декора — до центра.
2. Схема мебели, приборов и декора не является технической документацией для производства мебели; габариты — по паспортам изделий.
3. Облицовка — по сетке швов, раскладка от оси стены (треугольник у пола); подрезки — по листу раскладки плитки.
4. Гидроизоляция в 2 слоя, заход на стены 200 мм — до облицовки, с актом скрытых работ и тестом проливом (узел — на листе узлов).
5. Двери скрытого монтажа — полотно в плоскости стены, отделка стены по полотну, плинтус прерывается у короба (узел — на листе узлов).

**Допущения и предложения на листе**

Основа листа: размеры сняты с плана заказчика, контрольный обмер не выполнен (К-5); высота потолка 2700 мм принята: на плане заказчика не указана (К-5); подрайон климата не задан — принят не северный (жилые от 2,5 м) (К-4); толщины стен приняты: наружные 250 мм, перегородки 120 мм — не обмерены (К-5); разрешённая мощность 15 кВт принята по типовой квартире, технических условий нет (К-6).

См. лист открытых вопросов (лист 6, записи К-4–К-6).

1000 мм · печать 1:1

| Изм. | Кол.уч | Лист | № док. | Подп. | Дата |
|---|---|---|---|---|---|
| Разраб. | | Кырлан А.С. | | | 04.11.26 |
| Пров. | | | | | |
| ГИП | | | | | |
| | | | | | |
| Н. контр. | | | | | |
| Утв. | | | | | |

**ГД-2026-006-АИ**

Квартира 58 м²

Общая площадь 55,23* м² · * размеры приняты, не замерены (реестр — л. 6, 7, К-5)

Дизайн-проект интерьера

| Стадия | Лист | Листов |
|---|---|---|
| РП | 73 | 87 |

**Развёртки стен А, Б, В. Санузел (пом. 4)**

М 1:25

**Кырлан Александр Сергеевич**


выпуск 04.11.2026 № 3da8f16a26 · стр. 81 из 96

# Развёртка стены Г. Санузел (пом. 4)

Санузел (пом. 4) · вид изнутри помещения · размеры в мм, отметки в м


**ПРЕДВАРИТЕЛЬНО · не для производства работ · открыто пунктов: 10 (реестр — л. 6, 7)**

## Развёртка стены Г

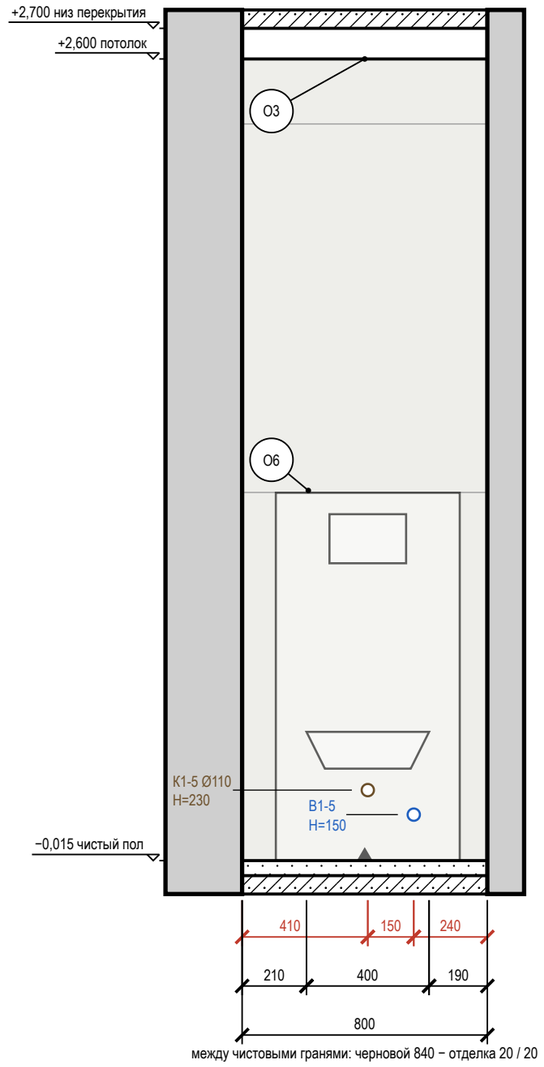


между чистовыми гранями: черновой 840 − отделка 20 / 20

## Схема развёрток (М 1:100)

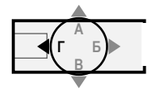


## Условные обозначения

- вывод В1 (код — в ведомости привязок)
- вывод К1 (код — в ведомости привязок)
- привязки точек и выводов от угла и от пола, мм
- мебель и приборы — фасад по расстановке (условно)
- стены и перекрытия в сечении
- плитка: сетка швов по формату, ▲ — ось старта
- О1 — марка отделки по реестру отделки альбома
- А — марка развёртки: буква стены, стрелка — взгляд

## Ведомость отделки (на листе)

| Марка | Поверхность | Материал, изделие | Цвет, код | Кол. |
|---|---|---|---|---|
| О3 | потолок | окраска, Tikkurila, глубокоматовая | NCS S 0300-N | 1,8 м² |
| О6 | стены | облицовка плиткой, Italon Charme Extra, 600×1200 мм, 610015000370 | Italon 610015000370 «Charme Extra» | 2,1 м² |

**Допущения и предложения на листе**

Основа листа: размеры сняты с плана заказчика, контрольный обмер не выполнен (К-5); высота потолка 2700 мм принята: на плане заказчика не указана (К-5); подрайон климата не задан — принят не северный (жилые от 2,5 м) (К-4); толщины стен приняты: наружные 250 мм, перегородки 120 мм — не обмерены (К-5); разрешённая мощность 15 кВт принята по типовой квартире, технических условий нет (К-6).

См. лист открытых вопросов (лист 6, записи К-4–К-6).

## Примечания

1. Развёртки — вид на стену изнутри помещения, по часовой стрелке; расположение — на схеме листа и на листе 60; размеры — в мм по чистовым поверхностям; отметки — в м от ±0,000; высоты Н — от чистого пола помещения до оси изделия, у декора — до центра.
2. Красная цепочка — привязки электроточек и выводов по осям от угла чистовых стен; высота Н — у знака, от чистого пола до оси; высоты мебели, проёмов и границ отделки — колонкой отметок слева. Стена с 5 и более точками или с мелкими звеньями привязок показана двумя видами: архитектурная развёртка (мебель, отделка, проёмы, высоты) и вид «Привязки» на отдельном листе — точки и выводы с марками, одна цепочка по осям и таблица привязок (каждая точка — строка).
3. У знака электроточки: марка (Р — розетка, S — выключатель, Св — светильник, ЭВ — вывод кабеля), ×N — число постов в рамке, гр. — группа щита, Н — высота оси от чистого пола, мм; группы по клавишам выключателя — на листе выключателей.
4. Схема мебели, приборов и декора не является технической документацией для производства мебели; габариты — по паспортам изделий (* — высота не задана в проекте, показана по типовому изделию).
5. Облицовка — по сетке швов, раскладка от оси стены (треугольник у пола); подрезки — по листу раскладки плитки.
6. Гидроизоляция в 2 слоя, заход на стены 200 мм — до облицовки, с актом скрытых работ и тестом проливом (узел — на листе узлов).

1000 мм · печать 1:1

| Изм. | Кол.уч | Лист | № док. | Подп. | Дата |
|---|---|---|---|---|---|
| Разраб. | | Кырлан А.С. | | | 04.11.26 |
| Пров. | | | | | |
| ГИП | | | | | |
| | | | | | |
| Н. контр. | | | | | |
| Утв. | | | | | |

**ГД-2026-006-АИ**

Квартира 58 м²

Общая площадь 55,23* м² · * размеры приняты, не замерены (реестр — л. 6, 7, К-5)

Дизайн-проект интерьера

| Стадия | Лист | Листов |
|---|---|---|
| РП | 74 | 87 |

**Развёртка стены Г. Санузел (пом. 4)**

М 1:20

**Кырлан Александр Сергеевич**


выпуск 04.11.2026 № 3da8f16a26 · стр. 82 из 96

# Развёртки стен А, Б. Прихожая (пом. 5)

Прихожая (пом. 5) · вид изнутри помещения · размеры в мм, отметки в м


ПРЕДВАРИТЕЛЬНО · не для производства работ · открыто пунктов: 10 (реестр — л. 6, 7)

## Развёртка стены А

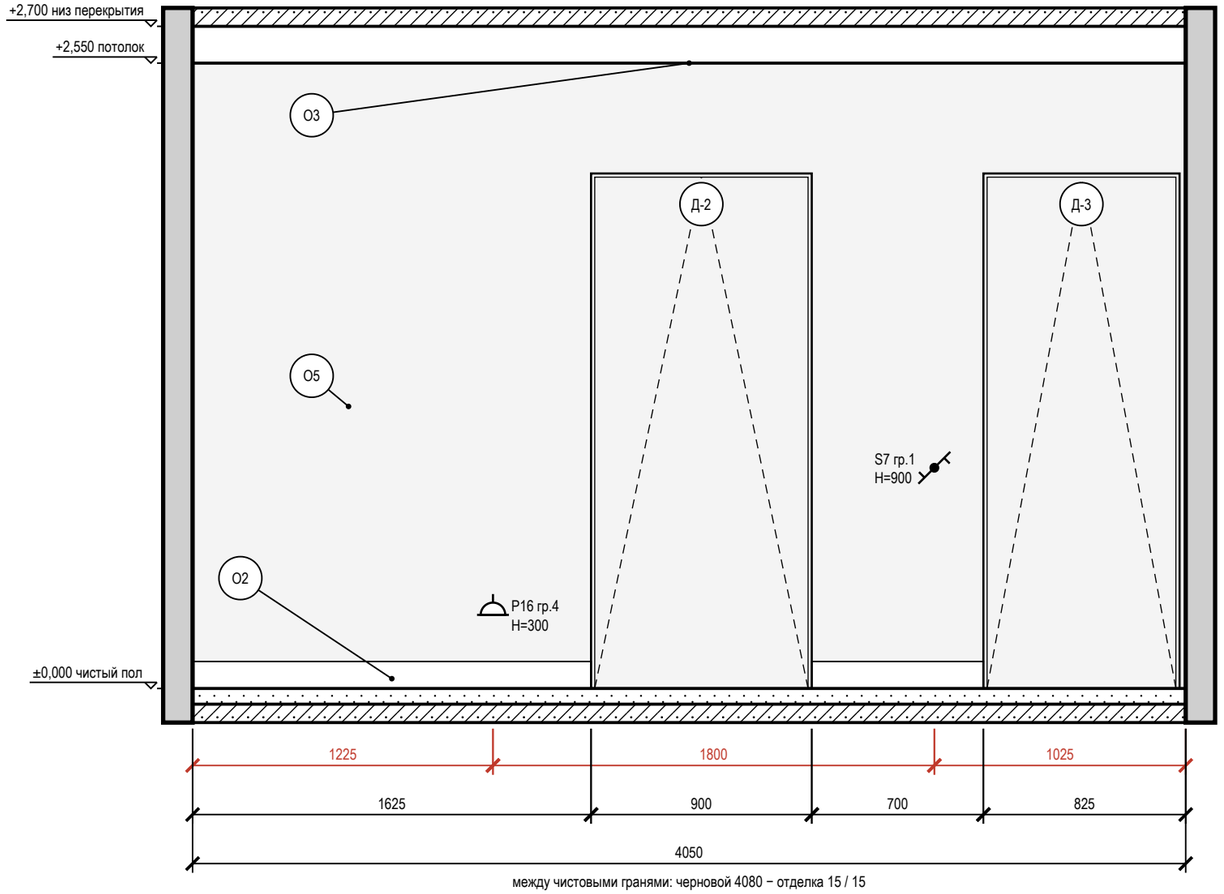



между чистовыми гранями: черновой 4080 − отделка 15 / 15

## Развёртка стены Б

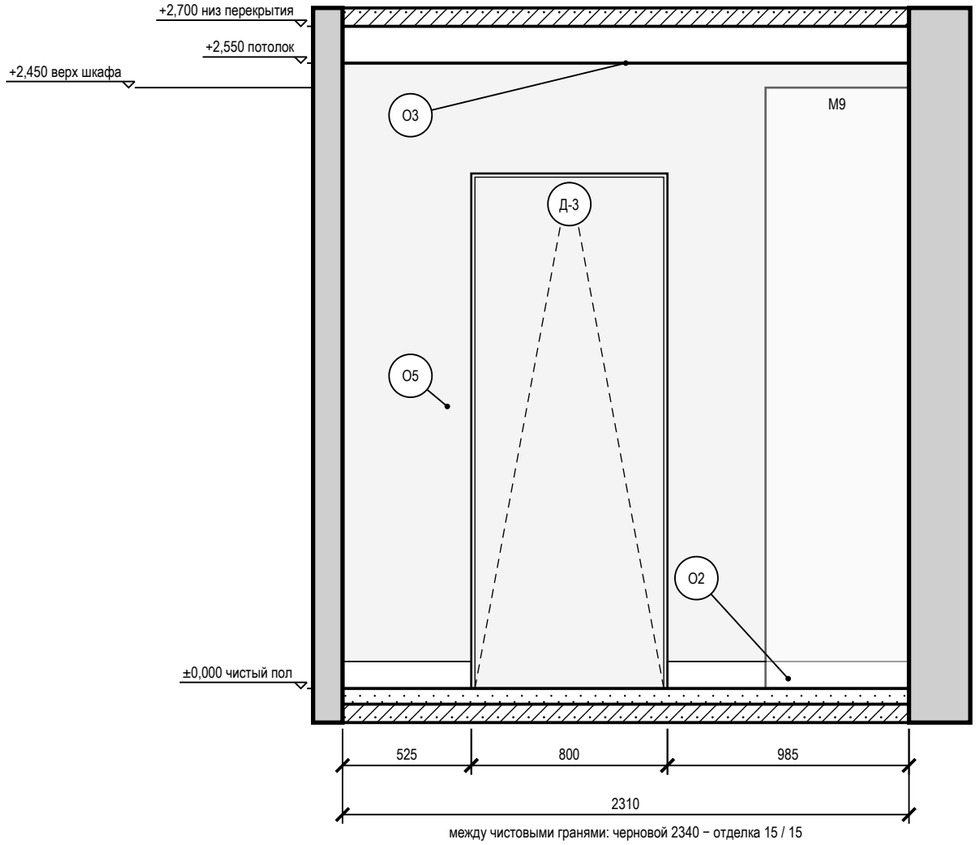


между чистовыми гранями: черновой 2340 − отделка 15 / 15

### Схема развёрток (М 1:100)

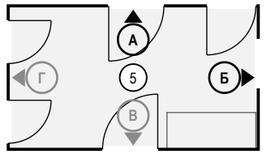


### Условные обозначения

- розетка с заземляющим контактом; у знака — марка, ×N постов в рамке, гр. — группа щита, Н — высота оси, мм
- выключатель одноклавишный
- выключатель с проходной или перекрёстной клавишей (обратный флажок); тип клавиши — в подписи
- привязки точек и выводов от угла и от пола, мм
- мебель и приборы — фасад по расстановке (условно)
- дверь скрытого монтажа: полотно в плоскости стены (узел — на листе узлов)
- стены и перекрытия в сечении
- О1 — марка отделки по реестру отделки альбома
- А — марка развёртки: буква стены, стрелка — взгляд

### Ведомость отделки (на листе)

| Марка | Поверхность | Материал, изделие | Цвет, код | Кол. |
|---|---|---|---|---|
| О2 | плинтус | плинтус МДФ, Orac Decor Luxxus, h 110 мм, SX184, шелковисто-матовая | NCS S 0300-N | 3,8 м |
| О3 | потолок | окраска, Tikkurila, глубокоматовая | NCS S 0300-N | 9,6 м² |
| О5 | стены | окраска, Tikkurila, шелковисто-матовая, подготовка Q3 | NCS S 1502-Y50R | 11 м² |

Допущения и предложения на листе. Основа листа: размеры сняты с плана заказчика, контрольный обмер не выполнен (К-5); высота потолка 2700 мм принята: на плане заказчика не указана (К-5); подрайон климата не задан — принят не северный (жилые от 2,5 м) (К-4); толщины стен приняты: наружные 250 мм, перегородки 120 мм — не обмерены (К-5); разрешённая мощность 15 кВт принята по типовой квартире, технических условий нет (К-6). См. лист открытых вопросов (лист 6, записи К-4–К-6).

### Примечания

1. Развёртки — вид на стену изнутри помещения, по часовой стрелке; расположение — на схеме листа и на листе 60; размеры — в мм по чистовым поверхностям; отметки — в м от ±0,000; высоты Н — от чистого пола помещения до оси изделия, у декора — до центра.
2. Красная цепочка — привязки электроточек и выводов по осям от угла чистовых стен; высота Н — у знака, от чистого пола до оси; высоты мебели, проёмов и границ отделки — колонкой отметок слева. Стена с 5 и более точками или с мелкими звеньями привязок показана двумя видами: архитектурная развёртка (мебель, отделка, проёмы, высоты) и вид «Привязки» на отдельном листе — точки и выводы с марками, одна цепочка по осям и таблица привязок (каждая точка — строка).
3. У знака электроточки: марка (Р — розетка, S — выключатель, Св — светильник, ЭВ — вывод кабеля), ×N — число постов в рамке, гр. — группа щита, Н — высота оси от чистого пола, мм; группы по клавишам выключателя — на листе выключателей.
4. Схема мебели, приборов и декора не является технической документацией для производства мебели; габариты — по паспортам изделий.
5. Двери скрытого монтажа — полотно в плоскости стены, отделка стены по полотну, плинтус прерывается у короба (узел — на листе узлов).
6. Потолок — у каждой стены свой, по плану потолков (ПТ1); ступени — зоной, кромка короба перед нишей — тонкой линией; в поле потолка: ПТ2 +2,600.

1000 мм · печать 1:1

| Изм. | Кол.уч | Лист | № док. | Подп. | Дата |
|---|---|---|---|---|---|
| Разраб. | | Кырлан А.С. | | | 04.11.26 |
| Пров. | | | | | |
| ГИП | | | | | |
| | | | | | |
| Н. контр. | | | | | |
| Утв. | | | | | |

**ГД-2026-006-АИ**

Квартира 58 м²

Общая площадь 55,23* м² · * размеры приняты, не замерены (реестр — л. 6, 7, К-5)

Дизайн-проект интерьера

| Стадия | Лист | Листов |
|---|---|---|
| РП | 75 | 87 |

**Развёртки стен А, Б. Прихожая (пом. 5)**

М 1:25

**Кырлан Александр Сергеевич**


выпуск 04.11.2026 № 3da8f16a26 · стр. 83 из 96

# Развёртки стен В, Г. Прихожая (пом. 5)

Прихожая (пом. 5) · вид изнутри помещения · размеры в мм, отметки в м


ПРЕДВАРИТЕЛЬНО · не для производства работ · открыто пунктов: 10 (реестр — л. 6, 7)

## Развёртка стены В

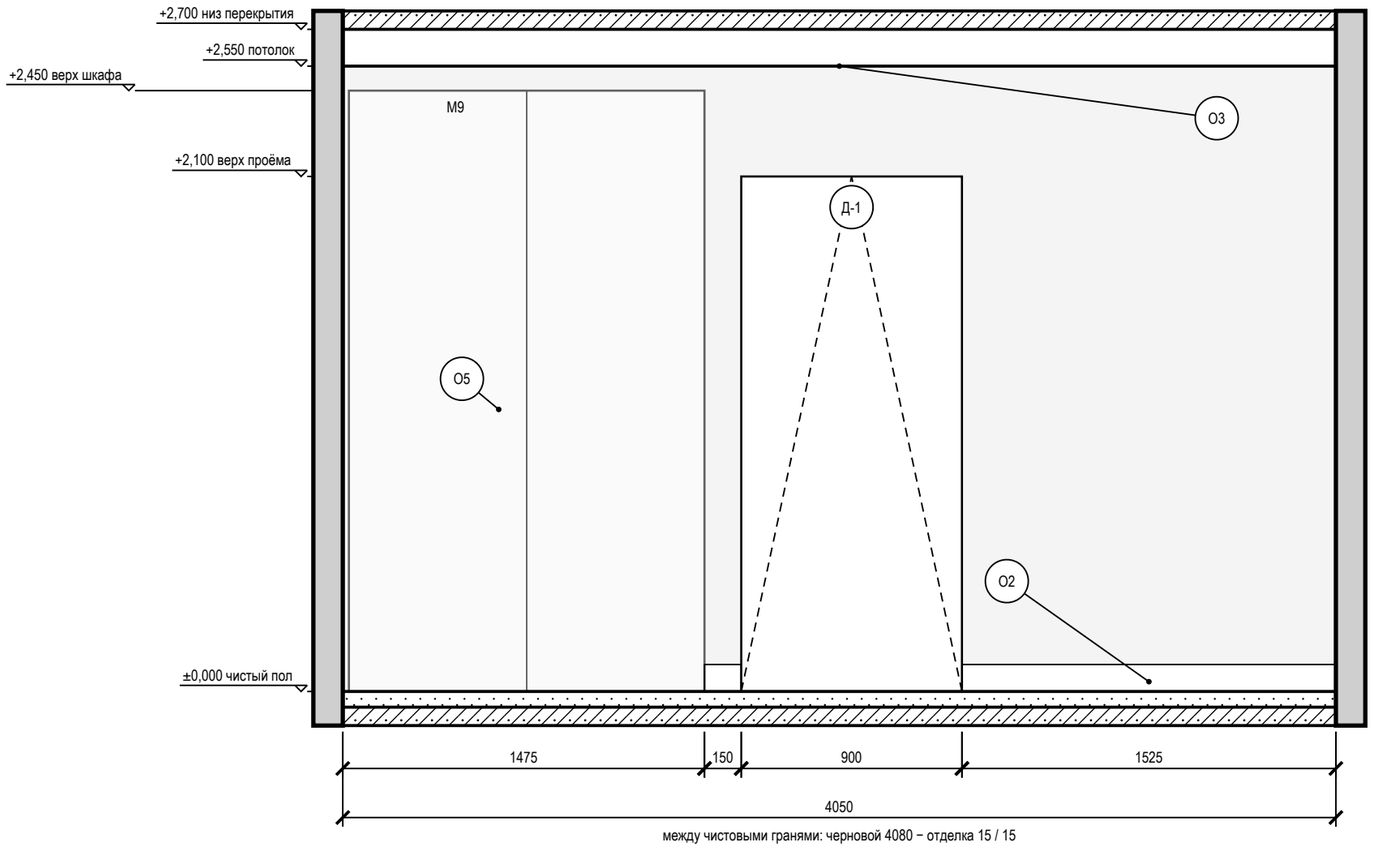



между чистовыми гранями: черновой 4080 − отделка 15 / 15

## Развёртка стены Г

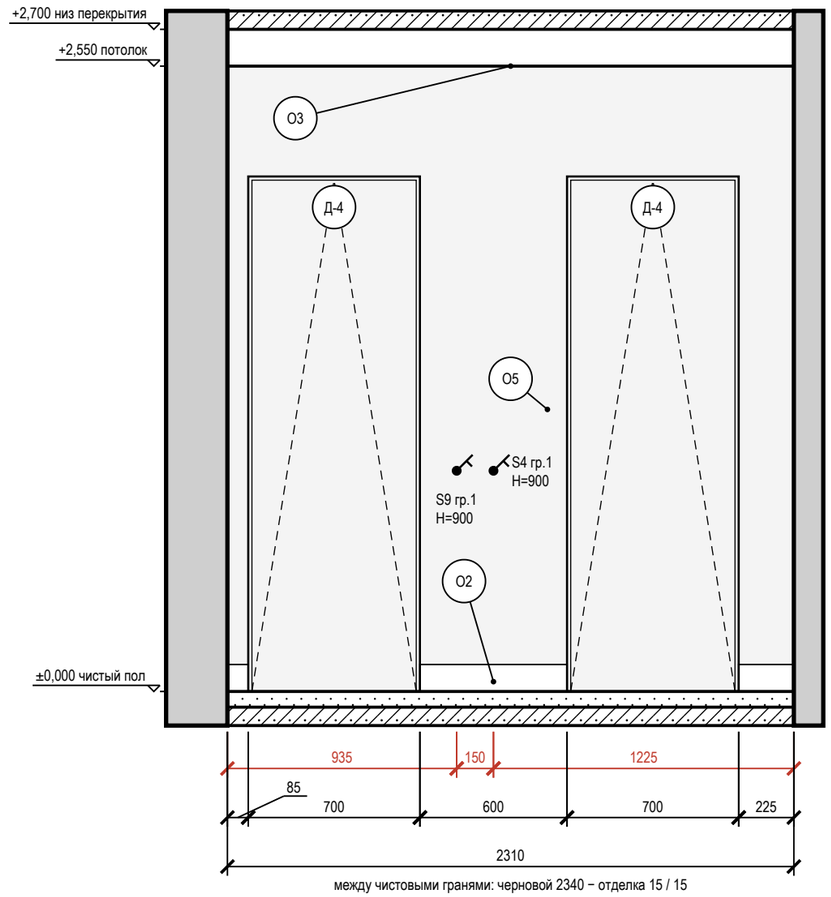


между чистовыми гранями: черновой 2340 − отделка 15 / 15

### Схема развёрток (М 1:100)

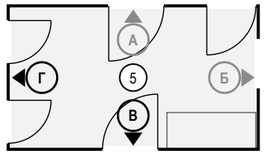


### Условные обозначения

- выключатель одноклавишный
- привязки точек и выводов от угла и от пола, мм
- мебель и приборы — фасад по расстановке (условно)
- дверь скрытого монтажа: полотно в плоскости стены (узел — на листе узлов)
- дверной проём; марка двери — в кружке
- стены и перекрытия в сечении
- О1 — марка отделки по реестру отделки альбома
- А — марка развёртки: буква стены, стрелка — взгляд

**Допущения и предложения на листе**

Основа листа: размеры сняты с плана заказчика, контрольный обмер не выполнен (К-5); высота потолка 2700 мм принята: на плане заказчика не указана (К-5); подрайон климата не задан — принят не северный (жилые от 2,5 м) (К-4); толщины стен приняты: наружные 250 мм, перегородки 120 мм — не обмерены (К-5); разрешённая мощность 15 кВт принята по типовой квартире, технических условий нет (К-6).
См. лист открытых вопросов (лист 6, записи К-4–К-6).

### Ведомость отделки (на листе)

| Марка | Поверхность | Материал, изделие | Цвет, код | Кол. |
|---|---|---|---|---|
| О2 | плинтус | плинтус МДФ, Orac Decor Luxxus, h 110 мм, SX184, шелковисто-матовая | NCS S 0300-N | 2,6 м |
| О3 | потолок | окраска, Tikkurila, глубокоматовая | NCS S 0300-N | 9,6 м² |
| О5 | стены | окраска, Tikkurila, шелковисто-матовая, подготовка Q3 | NCS S 1502-Y50R | 11,4 м² |

### Примечания

1. Развёртки — вид на стену изнутри помещения, по часовой стрелке; расположение — на схеме листа и на листе 60; размеры — в мм по чистовым поверхностям; отметки — в м от ±0,000; высоты Н — от чистого пола помещения до оси изделия, у декора — до центра.
2. Красная цепочка — привязки электроточек и выводов по осям от угла чистовых стен; высота Н — у знака, от чистого пола до оси; высоты мебели, проёмов и границ отделки — колонкой отметок слева. Стена с 5 и более точками или с мелкими звеньями привязок показана двумя видами: архитектурная развёртка (мебель, отделка, проёмы, высоты) и вид «Привязки» на отдельном листе — точки и выводы с марками, одна цепочка по осям и таблица привязок (каждая точка — строка).
3. Стена В показана двумя видами: здесь — архитектурная развёртка (мебель, отделка, проёмы, высоты), электроточки и выводы ВК с привязками и таблицей — на листе 77 («Привязки»).
4. У знака электроточки: марка (Р — розетка, S — выключатель, Св — светильник, ЭВ — вывод кабеля), ×N — число постов в рамке, гр. — группа щита, Н — высота оси от чистого пола, мм; группы по клавишам выключателя — на листе выключателей.
5. Схема мебели, приборов и декора не является технической документацией для производства мебели; габариты — по паспортам изделий.
6. Двери скрытого монтажа — полотно в плоскости стены, отделка стены по полотну, плинтус прерывается у короба (узел — на листе узлов).
7. Потолок — у каждой стены свой, по плану потолков (ПТ1); ступени — зоной, кромка короба перед нишей — тонкой линией; в поле потолка: ПТ2 +2,600.

1000 мм · печать 1:1

| Изм. | Кол.уч | Лист | № док. | Подп. | Дата |
|---|---|---|---|---|---|
| Разраб. | | Кырлан А.С. | | | 04.11.26 |
| Пров. | | | | | |
| ГИП | | | | | |
| | | | | | |
| Н. контр. | | | | | |
| Утв. | | | | | |

**ГД-2026-006-АИ**

Квартира 58 м²

Общая площадь 55,23* м² · * размеры приняты, не замерены (реестр — л. 6, 7, К-5)

Дизайн-проект интерьера

| Стадия | Лист | Листов |
|---|---|---|
| РП | 76 | 87 |

**Развёртки стен В, Г. Прихожая (пом. 5)**

М 1:25

**Кырлан Александр Сергеевич**


выпуск 04.11.2026 № 3da8f16a26 · стр. 84 из 96

# Привязки электроточек, стена В. Прихожая (пом. 5)

Прихожая (пом. 5) · вид изнутри помещения · привязки в мм, отметки в м · к развёртке на листе 76

ПРЕДВАРИТЕЛЬНО · не для производства работ · открыто пунктов: 10 (реестр — л. 6, 7)

## Развёртка стены В: электроточки и выводы

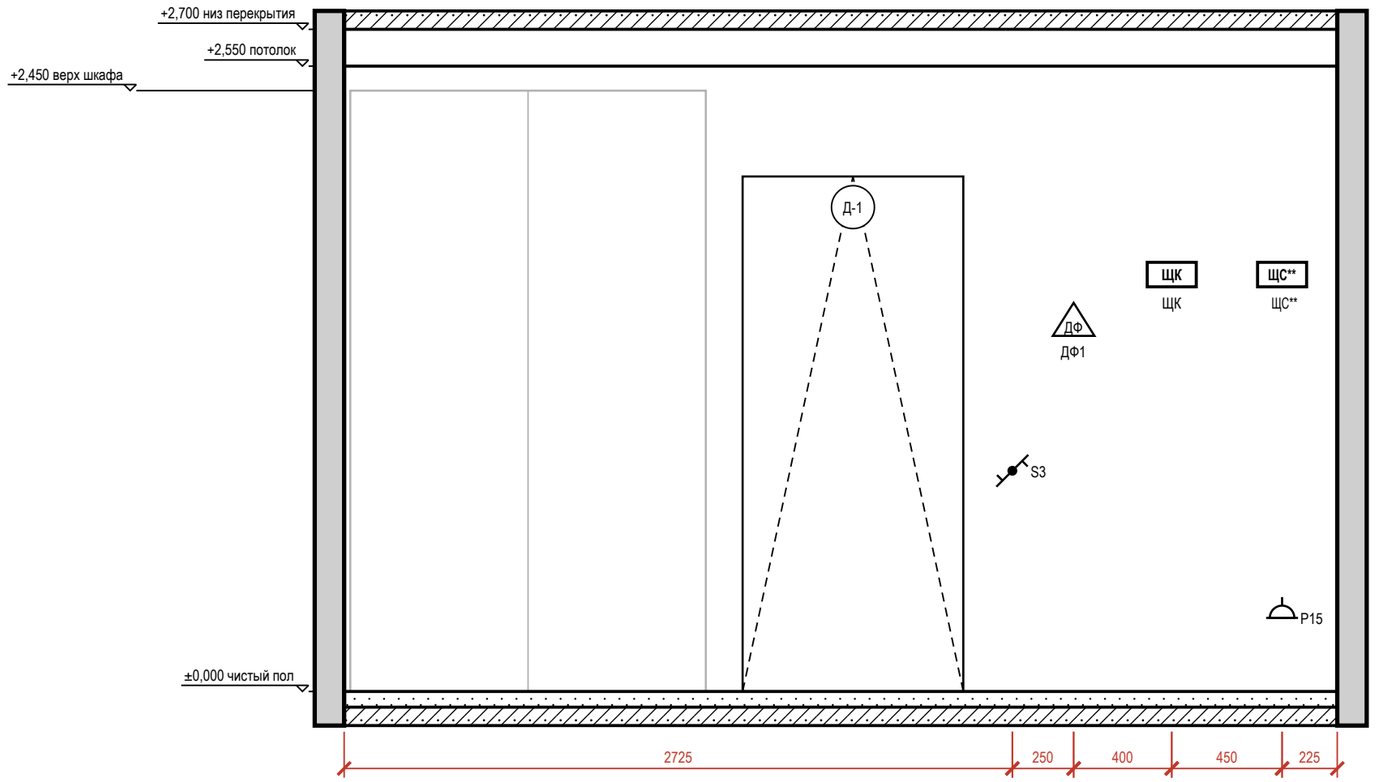



## Таблица привязок электроточек и выводов

| Марка | Назначение | От угла, мм | Н от пола, мм | Примечание |
|---|---|---|---|---|
| S3 | выключатель | 2725 | 900 | гр. 1 |
| ДФ1 | домофон: трубка домофона | 2975 | 1500 | |
| ЩК | щит | 3375 | 1700 | |
| P15 | розетка: питание ЩС** (роутер, ИБП) | 3825 | 300 | гр. 4 |
| ЩС** | щит: щит слаботочный: ввод провайдера, роутер | 3825 | 1700 | |

## Условные обозначения

- розетка с заземляющим контактом; у знака — марка, ×N постов в рамке, гр. — группа щита, Н — высота оси, мм
- выключатель одноклавишный
- выключатель с проходной или перекрёстной клавишей (обратный флажок); тип клавиши — в подписи
- ДФ — трубка или монитор домофона
- ЩК — щит квартирный
- привязки точек и выводов от угла и от пола, мм
- A — марка развёртки: буква стены, стрелка — взгляд

## Схема развёрток (М 1:50)

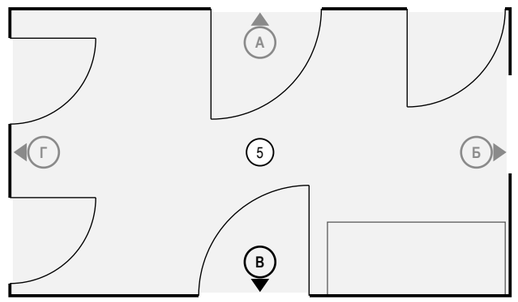


## Примечания

1. Вид «Привязки» стены В — электроточки и выводы ВК; архитектурная развёртка (мебель, отделка, проёмы, высоты) — на листе 76, расположение — на листе 60. Мебель и приборы — подложкой для ориентира; их марки и обозначения мебели, проёмов и стен — там же.
2. Привязки — в мм: по горизонтали от левого чистового угла стены до оси изделия, Н — от чистого пола до оси; все точки — в таблице привязок. Красная цепочка — привязки по осям; точки ближе 150 мм одна к другой в цепочку не дробятся — их привязки только в таблице.
3. У знака — марка электроточки (Р — розетка, S — выключатель, Св — светильник, ЭВ — вывод кабеля); посты в рамке и группа щита — в графе «Примечание»; группы по клавишам выключателя — на листе выключателей.

**Допущения и предложения на листе**

Основа листа: размеры сняты с плана заказчика, контрольный обмер не выполнен (К-5); высота потолка 2700 мм принята: на плане заказчика не указана (К-5); подрайон климата не задан — принят не северный (жилые от 2,5 м) (К-4); толщины стен приняты: наружные 250 мм, перегородки 120 мм — не обмерены (К-5); разрешённая мощность 15 кВт принята по типовой квартире, технических условий нет (К-6).

Знак «**» — предложение проектировщика, заказчиком не утверждено (согласовать с заказчиком): ЩС — щит слаботочный: место и состав.

См. лист открытых вопросов (лист 6, записи К-4–К-6).

1000 мм · печать 1:1

| Изм. | Кол.уч | Лист | № док. | Подп. | Дата |
|---|---|---|---|---|---|
| Разраб. | | Кырлан А.С. | | | 04.11.26 |
| Пров. | | | | | |
| ГИП | | | | | |
| Н. контр. | | | | | |
| Утв. | | | | | |

**ГД-2026-006-АИ**

Квартира 58 м²

Общая площадь 55,23* м² · * размеры приняты, не замерены (реестр — л. 6, 7, К-5)

Дизайн-проект интерьера

| Стадия | Лист | Листов |
|---|---|---|
| РП | 77 | 87 |

**Привязки электроточек, стена В. Прихожая (пом. 5)**

М 1:25

**Кырлан Александр Сергеевич**


выпуск 04.11.2026 № 3da8f16a26 · стр. 85 из 96

# Развёртки стен А, Б. Гардеробная (пом. 6)

Гардеробная (пом. 6) · вид изнутри помещения · размеры в мм, отметки в м


**ПРЕДВАРИТЕЛЬНО · не для производства работ · открыто пунктов: 10 (реестр — л. 6, 7)**

## Развёртка стены А

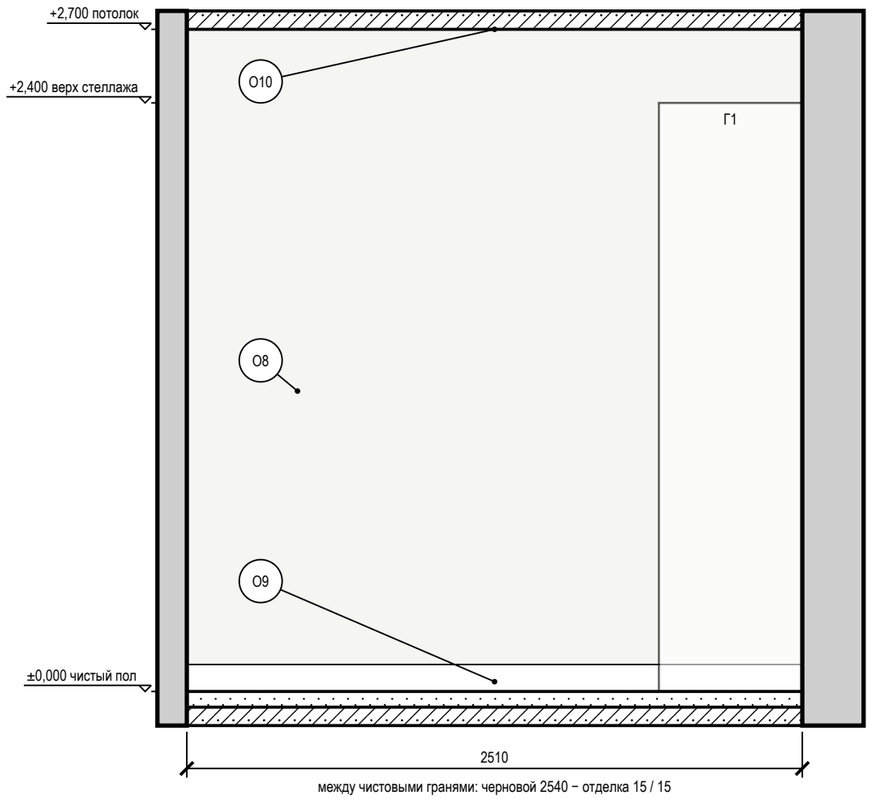


между чистовыми гранями: черновой 2540 − отделка 15 / 15

## Развёртка стены Б

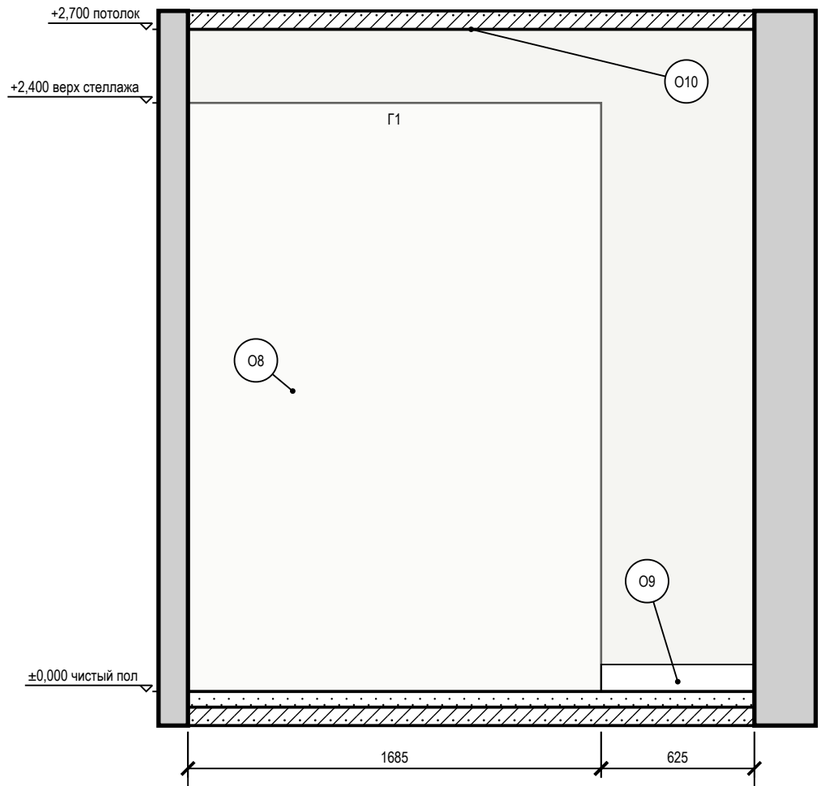



между чистовыми гранями: черновой 2340 − отделка 15 / 15

## Условные обозначения

- мебель и приборы — фасад по расстановке (условно)
- стены и перекрытия в сечении
- окраска: тон — цвет по коду производителя (условно)
- О1 — марка отделки по реестру отделки альбома
- А — марка развёртки: буква стены, стрелка — взгляд

## Схема развёрток (М 1:100)

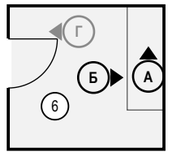


## Ведомость отделки (на листе)

| Марка | Поверхность | Материал, изделие | Цвет, код | Кол. |
|---|---|---|---|---|
| О8 | стены | окраска, Tikkurila Harmony, матовая, подготовка Q3 | Tikkurila V503 «Winter» | 13 м² |
| О9 | плинтус | плинтус МДФ, Orac Decor Luxxus, h 110 мм, SX184 | Tikkurila V503 «Winter» | 3,1 м |
| О10 | потолок | окраска, Tikkurila Anti-Reflex 2, глубокоматовая, подготовка Q3 | Tikkurila V503 «Winter» | 5,9 м² |

## Примечания

1. Развёртки — вид на стену изнутри помещения, по часовой стрелке; расположение — на схеме листа и на листе 60; размеры — в мм по чистовым поверхностям; отметки — в м от ±0,000; высоты Н — от чистого пола помещения до оси изделия, у декора — до центра.
2. Схема мебели, приборов и декора не является технической документацией для производства мебели; габариты — по паспортам изделий.

**Допущения и предложения на листе**

Основа листа: размеры сняты с плана заказчика, контрольный обмер не выполнен (К-5); высота потолка 2700 мм принята: на плане заказчика не указана (К-5); подрайон климата не задан — принят не северный (жилые от 2,5 м) (К-4); толщины стен приняты: наружные 250 мм, перегородки 120 мм — не обмерены (К-5); разрешённая мощность 15 кВт принята по типовой квартире, технических условий нет (К-6).

См. лист открытых вопросов (лист 6, записи К-4–К-6).

1000 мм · печать 1:1

| Изм. | Кол.уч | Лист | № док. | Подп. | Дата |
|---|---|---|---|---|---|
| Разраб. | | Кырлан А.С. | | | 04.11.26 |
| Пров. | | | | | |
| ГИП | | | | | |
| | | | | | |
| Н. контр. | | | | | |
| Утв. | | | | | |

**ГД-2026-006-АИ**

Квартира 58 м²

Общая площадь 55,23* м² · * размеры приняты, не замерены (реестр — л. 6, 7, К-5)

Дизайн-проект интерьера

| Стадия | Лист | Листов |
|---|---|---|
| РП | 78 | 87 |

**Развёртки стен А, Б. Гардеробная (пом. 6)**

М 1:25


**Кырлан Александр Сергеевич**

# Развёртка стены Г. Гардеробная (пом. 6)

Гардеробная (пом. 6) · вид изнутри помещения · размеры в мм, отметки в м


ПРЕДВАРИТЕЛЬНО · не для производства работ · открыто пунктов: 10 (реестр — л. 6, 7)

## Развёртка стены Г

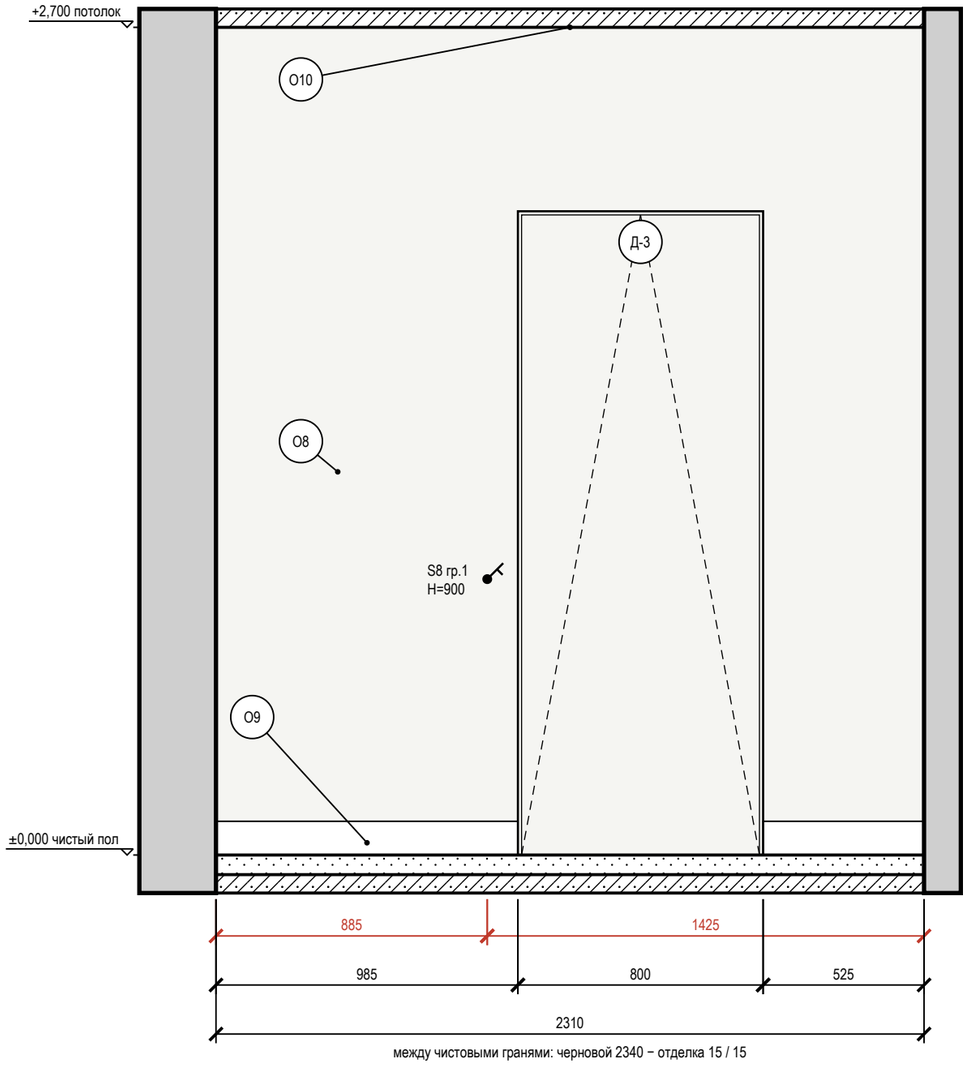


между чистовыми гранями: черновой 2340 − отделка 15 / 15

## Схема развёрток (М 1:100)

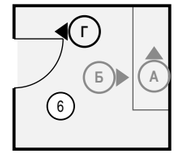


## Условные обозначения

- выключатель одноклавишный
- привязки точек и выводов от угла и от пола, мм
- мебель и приборы — фасад по расстановке (условно)
- дверь скрытого монтажа: полотно в плоскости стены (узел — на листе узлов)
- стены и перекрытия в сечении
- окраска: тон — цвет по коду производителя (условно)
- О1 — марка отделки по реестру отделки альбома
- А — марка развёртки: буква стены, стрелка — взгляд

## Ведомость отделки (на листе)

| Марка | Поверхность | Материал, изделие | Цвет, код | Кол. |
|---|---|---|---|---|
| О8 | стены | окраска, Tikkurila Harmony, матовая, подготовка Q3 | Tikkurila V503 «Winter» | 4,6 м² |
| О9 | плинтус | плинтус МДФ, Orac Decor Luxxus, h 110 мм, SX184 | Tikkurila V503 «Winter» | 1,5 м |
| О10 | потолок | окраска, Tikkurila Anti-Reflex 2, глубокоматовая, подготовка Q3 | Tikkurila V503 «Winter» | 5,9 м² |

**Допущения и предложения на листе**

Основа листа: размеры сняты с плана заказчика, контрольный обмер не выполнен (К-5); высота потолка 2700 мм принята: на плане заказчика не указана (К-5); подрайон климата не задан — принят не северный (жилые от 2,5 м) (К-4); толщины стен приняты: наружные 250 мм, перегородки 120 мм — не обмерены (К-5); разрешённая мощность 15 кВт принята по типовой квартире, технических условий нет (К-6).

См. лист открытых вопросов (лист 6, записи К-4–К-6).

## Примечания

1. Развёртки — вид на стену изнутри помещения, по часовой стрелке; расположение — на схеме листа и на листе 60; размеры — в мм по чистовым поверхностям; отметки — в м от ±0,000; высоты Н — от чистого пола помещения до оси изделия, у декора — до центра.
2. Красная цепочка — привязки электроточек и выводов по осям от угла чистовых стен; высота Н — у знака, от чистого пола до оси; высоты мебели, проёмов и границ отделки — колонкой отметок слева. Стена с 5 и более точками или с мелкими звеньями привязок показана двумя видами: архитектурная развёртка (мебель, отделка, проёмы, высоты) и вид «Привязки» на отдельном листе — точки и выводы с марками, одна цепочка по осям и таблица привязок (каждая точка — строка).
3. У знака электроточки: марка (Р — розетка, S — выключатель, Св — светильник, ЭВ — вывод кабеля), ×N — число постов в рамке, гр. — группа щита, Н — высота оси от чистого пола, мм; группы по клавишам выключателя — на листе выключателей.
4. Схема мебели, приборов и декора не является технической документацией для производства мебели; габариты — по паспортам изделий.
5. Двери скрытого монтажа — полотно в плоскости стены, отделка стены по полотну, плинтус прерывается у короба (узел — на листе узлов).

1000 мм · печать 1:1

| Изм. | Кол.уч | Лист | № док. | Подп. | Дата |
|---|---|---|---|---|---|
| Разраб. | | Кырлан А.С. | | | 04.11.26 |
| Пров. | | | | | |
| ГИП | | | | | |
| Н. контр. | | | | | |
| Утв. | | | | | |

**ГД-2026-006-АИ**

Квартира 58 м²

Общая площадь 55,23* м² · * размеры приняты, не замерены (реестр — л. 6, 7, К-5)

Дизайн-проект интерьера

| Стадия | Лист | Листов |
|---|---|---|
| РП | 79 | 87 |

**Развёртка стены Г. Гардеробная (пом. 6)**

М 1:20

**Кырлан Александр Сергеевич**


выпуск 04.11.2026 № 3da8f16a26 · стр. 87 из 96

# Узлы

Пороги и стыки покрытий, скрытые двери, короба стояков, гидроизоляция, плинтус


### 1 Порог 15 мм: мокрая зона — смежное помещение (М 1:5)

Применение: двери Д-4; места — лист 60

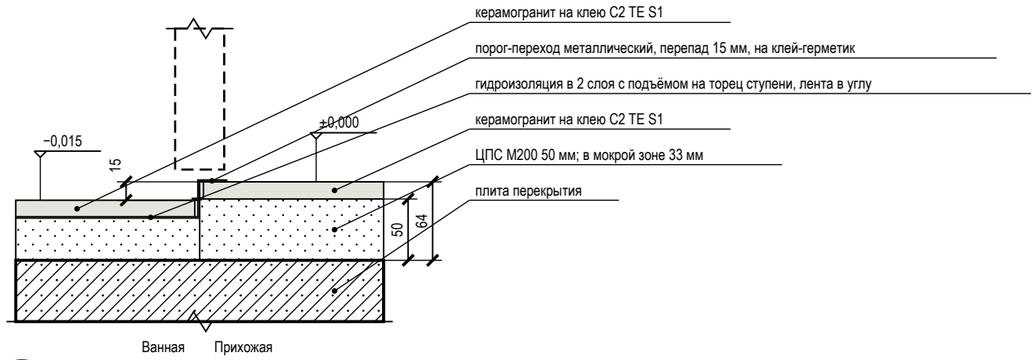



### 2 Дверь скрытого монтажа в плоскости стены, плинтус (М 1:5)

Применение: двери Д-2, Д-3, Д-4; места — лист 60

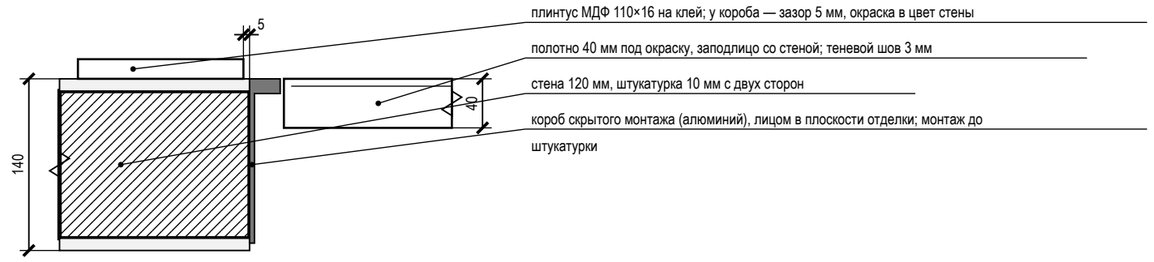



### 3 Короб стояков К1-1 с люком и звукоизоляцией (М 1:10)

Применение: пом. 3; места — лист 60

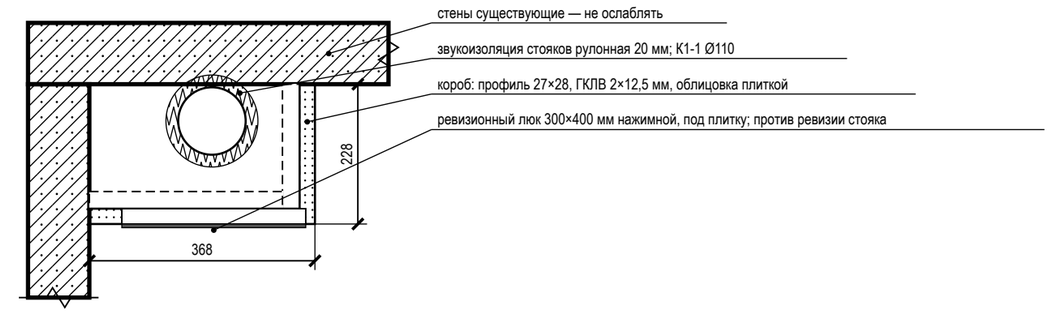



### 4 Гидроизоляция санузла: заход на стены 200 мм, примыкание ванны (М 1:20)

Применение: пом. 3, 4; места — лист 60

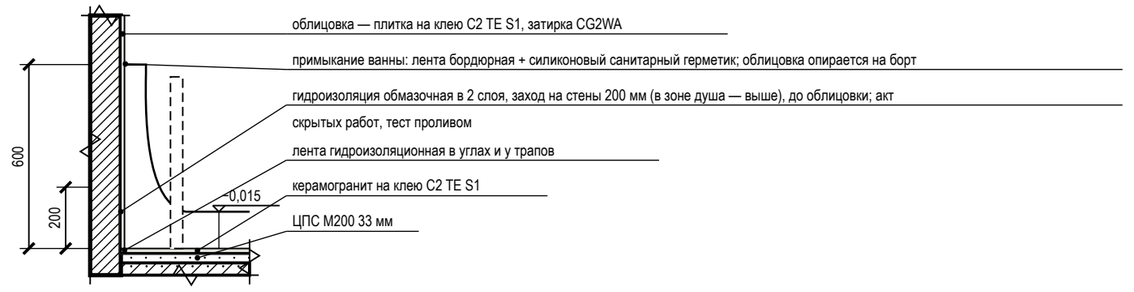



### 5 Плинтус МДФ 110×16 мм у окрашенной стены по доске (ламинату) (М 1:10)

Применение: пом. 1, 2, 6; места — лист 60

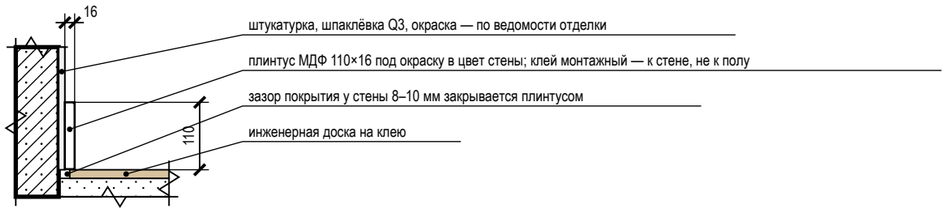


### 6 Плинтус МДФ 110×16 мм у окрашенной стены по керамограниту (плитке) (М 1:10)

Применение: пом. 5; места — лист 60

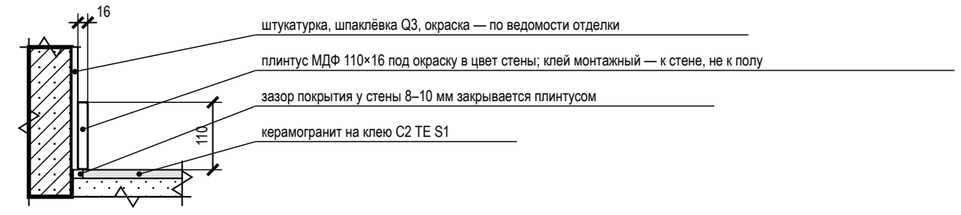


## Условные обозначения

- железобетон (плита, стены) — условно: конструкция не установлена
- кладка, перегородка — условно: конструкция не установлена
- стяжка, раствор
- гипсокартон ГКЛВ
- звукоизоляция, эластичный заполнитель
- плитка, керамогранит на клею
- инженерная доска (покрытие пола)
- металлический профиль (порог, Т-профиль, короб двери)
- гидроизоляция (обмазочная, лента)

## Примечания

1. Узлы — типовые решения проекта для мест, отмеченных выносками на листе схемы расположения развёрток и узлов; размеры — в мм, отметки — в м от ±0,000.
2. Узлы с гидроизоляцией, закладными и коробами скрытого монтажа принимаются по актам скрытых работ до закрытия отделкой; гидроизоляция — после теста проливом (24 ч).
3. Марки изделий (порог, Т-профиль, короб скрытой двери, люк) — по спецификациям; замена — на аналог с теми же габаритами по согласованию с автором проекта.
4. Материал плиты перекрытия и стен в узлах показан условно (железобетон, кладка): конструкция дома не установлена — крепёж, анкеры и толщины слоёв уточняются после обследования (до него — по допущениям общих указаний).

Допущения и предложения на листе. Основа листа: размеры сняты с плана заказчика, контрольный обмер не выполнен (К-5); высота потолка 2700 мм принята: на плане заказчика не указана (К-5); подрайон климата не задан — принят не северный (жилые от 2,5 м) (К-4); толщины стен приняты: наружные 250 мм, перегородки 120 мм — не обмерены (К-5); разрешённая мощность 15 кВт принята по типовой квартире, технических условий нет (К-6). См. лист открытых вопросов (лист 6, записи К-4–К-6).

| Изм. | Кол.уч | Лист | № док. | Подп. | Дата |
|---|---|---|---|---|---|
| Разраб. | | Кырлан А.С. | | | 04.11.26 |
| Пров. | | | | | |
| ГИП | | | | | |
| | | | | | |
| Н. контр. | | | | | |
| Утв. | | | | | |

**ГД-2026-006-АИ**

Квартира 58 м²

Общая площадь 55,23* м² · * размеры приняты, не замерены (реестр — л. 6, 7, К-5)

Дизайн-проект интерьера

| Стадия | Лист | Листов |
|---|---|---|
| РП | 80 | 87 |

**Узлы**

М 1:5; 1:10; 1:20

**Кырлан Александр Сергеевич**

выпуск 04.11.2026 № 3da8f16a26 · стр. 88 из 96

09

# Смета

Кырлан Александр Сергеевич

выпуск 04.11.2026 · 3da8f16a26 · стр. 89 из 96

# Ведомость объёмов работ

ПРЕДВАРИТЕЛЬНО · не для производства работ · открыто пунктов: 10 (реестр — л. 6, 7)

Объёмы по помещениям от чертежа · площади в м², длины в м · формула, правило проёмов и источник в каждой строке

## Ведомость объёмов работ по помещениям

| Поз. | Наименование работ (материал, число слоёв) | Ед. изм. | Объём по помещениям (№ по экспликации) | | | | | | Всего | Формула подсчёта | Правило проёмов | Источник | Цена за ед., ₽ | Стоимость, ₽ |
|---|---|---|---|---|---|---|---|---|---|---|---|---|---|---|
| | | | 1 | 2 | 3 | 4 | 5 | 6 | | | | | | |
| **1. Демонтаж и черновые работы** | | | | | | | | | | | | | | |
| 1 | Демонтаж существующего покрытия пола до основания | м² | 21,04 | 13,95 | 2,95 | 1,80 | 9,55 | 5,94 | 55,23 | S пом. | | л. 14, 15 | по КП | |
| 2 | Демонтаж существующей отделки стен до основания | м² | 41,25 | 33,91 | 16,94 | 14,12 | 22,66 | 24,67 | 153,55 | P × H − проёмы | за вычетом проёмов | л. 14, 15 | по КП | |
| 3 | Демонтаж существующей отделки потолка до основания | м² | 21,04 | 13,95 | 2,95 | 1,80 | 9,55 | 5,94 | 55,23 | S пом. | | л. 14, 15 | по КП | |
| 4 | Демонтаж существующих дверных блоков | шт | | | | | 5 | 1 | 6 | по ведомости проёмов | | л. 15, 16 | по КП | |
| 5 | Демонтаж существующих сантехприборов и электрооборудования (если есть) | компл | | | | | | | | по факту на объекте | | л. 15 | по КП | |
| 6 | Устройство стяжки: стяжка ЦПС М200, 50 мм | м² | 21,09 | 14,00 | 2,99 | 1,84 | 9,90 | 5,99 | 55,81 | S пом. + S в дверных проёмах (b × t/2) | проёмы добавлены | л. 47, 48 | 530 | 29 579 |
| 7 | Гидроизоляция обмазочная, 2 слоя: пол, стены на 200 мм, зоны замачивания | м² | | | 4,22 | 2,85 | | | 7,07 | пол + (P − двери) × h заведения + зоны замачивания | | л. 43 | 450 | 3 182 |
| 8 | Штукатурка стен по маякам, до 10 мм | м² | | | | | | 24,67 | 24,67 | P × H − проёмы по обводу коробок − грани перегородок на ГКЛВ | за вычетом проёмов | л. 14, 48 | 530 | 13 075 |
| 9 | Штукатурка оконных откосов шириной до 200 мм | м² | 1,73 | 0,86 | | | | | 2,59 | Σ (2h + b) × глубина откоса | откосы ≤ 200 мм | л. 14 | 540 | 1 399 |
| 10 | Потолок ГКЛ по каркасу П113, 1 слой | м² | 21,04 | 13,95 | 2,95 | 1,80 | 9,55 | | 49,29 | S пом. по плану потолков | | л. 40–42 | 1 500 | 73 935 |
| **Итого по разделу 1 — 121 170 ₽ (позиций 10, из них по КП 5); в сводную смету — л. 86, 87** | | | | | | | | | | | | | | |
| **2. Инженерные системы** | | | | | | | | | | | | | | |
| 11 | Прокладка слаботочной линии: Кабель домофона — тип по системе поставщика, отдельно от силовых | м | | | | | | | 3,40 | по лучам от ЩС**: 1 точ., запас 10 % | | л. 26 | по КП | |
| 12 | Прокладка слаботочной линии: Кабель коаксиальный RG-6 (75 Ом) к розеткам ТВ, отдельно от силовых | м | | | | | | | 16,30 | по лучам от ЩС**: 1 точ., запас 10 % | | л. 26 | по КП | |
| 13 | Прокладка слаботочной линии: Кабель U/UTP кат. 5e (LAN, Wi-Fi и камеры по PoE), отдельно от силовых | м | | | | | | | 30,10 | по лучам от ЩС**: 2 точ., запас 10 % | | л. 26 | по КП | |
| 14 | Прокладка гофротрубы Ø20 для слаботочных линий, отдельно от силовых | м | | | | | | | 44,80 | по длине лучей без участков в канале плинтуса (≈ 90 %) | | л. 26 | по КП | |
| 15 | Сборка слаботочного щита ЩС**: корпус, патч-панель, подключение линий и питания 220 В; коммутатор и точки доступа — оборудование заказчика | шт | | | | | | | 1 | один щит | | л. 23, 26 | по КП | |
| 16 | Электроточка: подрозетник в бетоне, розетка, выключатель, вывод | шт | 16 | 6 | 3 | | 7 | 1 | 33 | по ведомости электроточек | | л. 20, 23 | 950 | 31 350 |
| 17 | Штробы в стенах под спуски кабеля к точкам — выполняются только после технического заключения о несущих стенах | м | 30,00 | 11,70 | 3,35 | | 12,15 | 1,80 | 59,00 | Σ (H − h) по точкам на стенах: вертикальные спуски | после техзаключения | л. 15, 20 | по КП | |
| 18 | Установка встраиваемого точечного светильника | шт | | | 1 | 1 | 2 | | 4 | по плану освещения | | л. 21 | 750 | 3 000 |
| 19 | Монтаж светильника: потолочного, подвесного, настенного | шт | 2 | 4 | 1 | | | 1 | 8 | по плану освещения | | л. 21 | 1 200 | 9 600 |
| 20 | Монтаж LED-ленты в алюминиевый профиль | м | 1,80 | | | | | | 1,80 | Σ длин лент по плану освещения | | л. 21 | 230 | 414 |
| 21 | Установка блока питания LED в доступном месте (люк, шкаф) | шт | 1 | 1 | | | | | 2 | один на LED-группу | | л. 21 | 570 | 1 140 |
| 22 | Установка автономного пожарного извещателя | шт | 1 | 1 | | | 1 | | 3 | по плану розеток | | л. 20 | по КП | |
| 23 | Сборка щита: установка автоматов и АВДТ групп, вводного автомата | шт | | | | | | | 7 | группы + вводной автомат | | л. 24 | 230 | 1 610 |

**Допущения и предложения на листе**

Основа листа: размеры сняты с плана заказчика, контрольный обмер не выполнен (К-5); высота потолка 2700 мм принята: на плане заказчика не указана (К-5); подрайон климата не задан — принят не северный (жилые от 2,5 м) (К-4); толщины стен приняты: наружные 250 мм, перегородки 120 мм — не обмерены (К-5); разрешённая мощность 15 кВт принята по типовой квартире, технических условий нет (К-6).

Знак «**» — предложение проектировщика, заказчиком не утверждено (согласовать с заказчиком): ЩС — щит слаботочный: место и состав.

См. лист открытых вопросов (лист 6, записи К-4–К-6).

| Изм. | Кол.уч | Лист | № док. | Подп. | Дата |
|---|---|---|---|---|---|
| Разраб. | | Кырлан А.С. | | | 04.11.26 |
| Пров. | | | | | |
| ГИП | | | | | |
| | | | | | |
| Н. контр. | | | | | |
| Утв. | | | | | |

**ГД-2026-006-АИ**

Квартира 58 м²

Общая площадь 55,23* м² · * размеры приняты, не замерены (реестр — л. 6, 7, К-5)

Дизайн-проект интерьера

| Стадия | Лист | Листов |
|---|---|---|
| РП | 81 | 87 |

**Ведомость объёмов работ**

М б/м

**Кырлан Александр Сергеевич**

# Ведомость объёмов работ (продолжение)

Объёмы по помещениям от чертежа · площади в м², длины в м · формула, правило проёмов и источник в каждой строке

## Ведомость объёмов работ по помещениям (продолжение)

| Поз. | Наименование работ (материал, число слоёв) | Ед. изм. | Объём по помещениям (№ по экспликации) | | | | | | Всего | Формула подсчёта | Правило проёмов | Источник | Цена за ед., ₽ | Стоимость, ₽ |
|---|---|---|---|---|---|---|---|---|---|---|---|---|---|---|
| | | | 1 | 2 | 3 | 4 | 5 | 6 | | | | | | |
| 24 | Установка вводного УЗО | шт | | | | | | | 1 | по однолинейной схеме | | л. 24 | 380 | 380 |
| 25 | Монтаж инсталляции, установка подвесного унитаза и кнопки смыва | шт | | | | 1 | | | 1 | по плану выводов | | л. 29, 38 | 10 500 | 10 500 |
| 26 | Короб инсталляции: каркас и обшивка ГКЛВ в 2 слоя, ревизионный доступ к смыву | шт | | | | 1 | | | 1 | по плану выводов | | л. 29, 43–46 | по КП | |
| 27 | Короб стояков Ш1 489 × 319 мм (внутренний 436 × 266): каркас и обшивка ГКЛВ в 2 слоя, ревизионный люк 300 × 400 | м² | | | 2,11 | | | | 2,11 | свободный периметр короба × H помещения | | л. 14, 29 | по КП | |
| 28 | Короб К1 над чистым полом: каркас и обшивка ГКЛВ под плитку (материалы — в спецификации ВК) | м.п. | 0,40 | | 0,76 | 0,30 | | | 1,46 | Σ открытых участков выпусков К1 (профиль листа разводки ВК) | | л. 29, 38 | по КП | |
| 29 | Установка ванны с сифоном | шт | | | 1 | | | | 1 | по плану выводов | | л. 29, 38 | 6 000 | 6 000 |
| 30 | Установка умывальника (мойки) с сифоном и смесителем | шт | 1 | | 1 | | | | 2 | по плану выводов | | л. 29, 38 | 3 000 | 6 000 |
| 31 | Подключение стиральной (посудомоечной) машины к ВК | шт | 1 | | | | | | 1 | по плану выводов | | л. 29 | по КП | |
| 32 | Установка радиатора с узлом подключения и терморегулятором | шт | 2 | 1 | | | | | 3 | по плану отопления | | л. 28 | по КП | |
| **Итого по разделу 2 — 69 994 ₽ (позиций 22, из них по КП 12); в сводную смету — л. 86, 87** | | | | | | | | | | | | | | |
| **3. Чистовые работы** | | | | | | | | | | | | | | |
| 33 | Облицовка стен керамогранитом 1200×600 на клею | м² | | | 14,95 | 13,40 | | | 28,35 | по раскладке: зона облицовки − место за коробом | за вычетом проёмов | л. 43–46 | 2 500 | 70 875 |
| 34 | Облицовка короба инсталляции (ГКЛВ) керамогранитом: лицо, боковины, полка | м² | | | 1,99 | 1,47 | | | 3,46 | по раскладке: лицо, боковины, полка | | л. 43–46 | 2 500 | 8 650 |
| 35 | Укладка керамогранита на пол, 600×600, на клею | м² | | | 2,99 | 1,84 | 9,90 | | 14,73 | S пом. + S в дверных проёмах | проёмы добавлены | л. 43–47 | 1 800 | 26 514 |
| 36 | Затирка швов керамогранита | м² | | | 19,89 | 16,67 | 9,55 | | 46,11 | Σ S облицовки и пола из плитки | | л. 43–46 | 150 | 6 917 |
| 37 | Грунтование стен, 2 слоя (под штукатурку и под отделку) | м² | 41,25 | 33,91 | 16,94 | 14,12 | 22,66 | 24,67 | 153,55 | P × H − проёмы | за вычетом проёмов | л. 48 | 96 | 14 741 |
| 38 | Шпаклёвка стен под окраску, 2 слоя (старт и финиш), уровень Q3 | м² | 41,25 | 33,91 | | | 22,66 | 24,67 | 122,49 | P × H − проёмы − фартук | за вычетом проёмов | л. 48 | 750 | 91 868 |
| 39 | Грунтование и шпаклёвка оконных откосов, 2 слоя | м.п. | 9,60 | 4,80 | | | | | 14,40 | Σ (2h + b) по окнам | по окнам | л. 14 | 300 | 4 320 |
| 40 | Грунтование потолка, 2 слоя | м² | 21,04 | 13,95 | 2,95 | 1,80 | 9,55 | 5,94 | 55,23 | S пом. | | л. 48 | 96 | 5 302 |
| 41 | Шпаклёвка потолка под окраску, 2 слоя, уровень Q3 | м² | 21,04 | 13,95 | 2,95 | 1,80 | 9,55 | 5,94 | 55,23 | S пом. | | л. 40–42, 48 | 950 | 52 469 |
| 42 | Окраска потолка водно-дисперсионной краской, 2 слоя | м² | 21,04 | 13,95 | 2,95 | 1,80 | 9,55 | 5,94 | 55,23 | S пом. | | л. 48 | 360 | 19 883 |
| 43 | Окраска стен водно-дисперсионной краской, 2 слоя | м² | 48,26 | 38,15 | | | 32,74 | 26,35 | 145,50 | P × H − фартук, проёмы не вычитаются | без вычета проёмов | л. 48 | 300 | 43 650 |
| 44 | Окраска оконных откосов, 2 слоя | м.п. | 9,60 | 4,80 | | | | | 14,40 | Σ (2h + b) по окнам | по окнам | л. 14 | 120 | 1 728 |
| 45 | Укладка инженерной доски на клей | м² | 21,09 | 14,00 | | | | 5,99 | 41,08 | S пом. + S в дверных проёмах | проёмы добавлены | л. 47, 48 | 1 200 | 49 296 |
| 46 | Установка плинтуса МДФ h=110 мм | м.п. | 17,66 | 14,16 | | | 8,04 | 8,96 | 48,82 | P − ширина дверных проёмов | | л. 48 | 450 | 21 969 |
| 47 | Окраска плинтуса в тоне S 0300-N, 2 слоя | м.п. | 17,66 | 14,16 | | | 8,04 | 8,96 | 48,82 | как плинтус | | л. 48 | 300 | 14 646 |
| 48 | Монтаж дверей скрытого монтажа под покраску (поставщик дверей) | шт | | | | | 4 | 1 | 5 | по ведомости проёмов | | л. 16 | 5 250 | 26 250 |
| 49 | Входная дверь, поставка с монтажом и откосами | шт | | | | | | | 1 | по ведомости проёмов | | л. 16 | по КП | |
| **Итого по разделу 3 — 459 078 ₽ (позиций 17, из них по КП 1); в сводную смету — л. 86, 87** | | | | | | | | | | | | | | |

**Допущения и предложения на листе**

Основа листа: размеры сняты с плана заказчика, контрольный обмер не выполнен (К-5); высота потолка 2700 мм принята: на плане заказчика не указана (К-5); подрайон климата не задан — принят не северный (жилые от 2,5 м) (К-4); толщины стен приняты: наружные 250 мм, перегородки 120 мм — не обмерены (К-5); разрешённая мощность 15 кВт принята по типовой квартире, технических условий нет (К-6).

См. лист открытых вопросов (лист 6, записи К-4–К-6).

| Изм. | Кол.уч | Лист | № док. | Подп. | Дата |
|---|---|---|---|---|---|
| Разраб. | | Кырлан А.С. | | | 04.11.26 |
| Пров. | | | | | |
| ГИП | | | | | |
| | | | | | |
| Н. контр. | | | | | |
| Утв. | | | | | |

**ГД-2026-006-АИ**

Квартира 58 м²

Общая площадь 55,23* м² · * размеры приняты, не замерены (реестр — л. 6, 7, К-5)

Дизайн-проект интерьера

| Стадия | Лист | Листов |
|---|---|---|
| РП | 82 | 87 |

**Ведомость объёмов работ (продолжение)**

М б/м

**Кырлан Александр Сергеевич**

# Ведомость объёмов работ (окончание)

Объёмы по помещениям от чертежа · площади в м², длины в м · формула, правило проёмов и источник в каждой строке

## Ведомость подсчёта площадей по помещениям

| № | Помещение | S пола, м² | P, м | H, м | P × H, м² | Проёмы, м² | Стены нетто, м² | В дверных проёмах, м² | Плинтус, м | Откосы, м.п. |
|---|---|---|---|---|---|---|---|---|---|---|
| 1 | Кухня-гостиная | 21,04 | 18,56 | 2,60 | 48,26 | 7,01 | 41,25 | 0,05 | 17,66 | 9,60 |
| 2 | Спальня | 13,95 | 14,96 | 2,55 | 38,15 | 4,24 | 33,91 | 0,05 | 14,16 | 4,80 |
| 3 | Ванная | 2,95 | 7,04 | 2,62 | 18,41 | 1,47 | 16,94 | 0,04 | нет | нет |
| 4 | Санузел | 1,80 | 5,96 | 2,62 | 15,59 | 1,47 | 14,12 | 0,04 | нет | нет |
| 5 | Прихожая | 9,55 | 12,84 | 2,55 | 32,74 | 10,08 | 22,66 | 0,35 | 8,04 | нет |
| 6 | Гардеробная | 5,94 | 9,76 | 2,70 | 26,35 | 1,68 | 24,67 | 0,05 | 8,96 | нет |
| | **Итого** | **55,23** | | | **179,49** | **25,95** | **153,54** | **0,58** | **48,82** | **14,40** |

## Реестр контрольных сумм

| Показатель | По ВОР | По чертежу | Расхождение | Лист |
|---|---|---|---|---|
| Σ площадей помещений без летних, м² — общая площадь по экспликации | 55,23 | 55,23 | 0,0 % | л. 14 |
| Стены под окраску, м² (шпаклёвка) ведомость отделки | 122,49 | 122,49 | 0,0 % | л. 48 |
| Потолки под окраску, м² — ведомость отделки | 55,23 | 55,23 | 0,0 % | л. 48 |
| Плинтус, м — ведомость отделки | 48,82 | 48,82 | 0,0 % | л. 48 |
| Плитка к заказу, шт — ведомость плитки | 152 | 152 | 0,0 % | л. 43 |
| Гидроизоляция, м² — ведомость материалов плитки | 7,07 | 12,21 | -42,1 % | л. 43 |
| Точки ЭОМ, шт — планы ЭОМ (без щитов) | 51 | 52 | -1,9 % | л. 20, 21 |

## Примечания

1. Объёмы — от геометрии проекта (та же, что на планах и в ведомости отделки), не от общей площади: P — периметр чистого контура, H — от чистого пола до низа потолка, проёмы — по наружному обводу коробок.
2. Подсчёт по ГЭСН-2001-15 и ГЭСН-2001-11: штукатурка и шпаклёвка стен — за вычетом проёмов; окраска водными составами — без вычета проёмов (п. 2.24); откосы — отдельно, по ширине до 200 и более 200 мм; полы — с площадью в дверных проёмах.
3. Плитка — по раскладке (целые и с подрезкой); короб инсталляции и фартук — отдельными строками, двойного счёта облицовки нет. Материалы, запас и количество к заказу — в спецификации материалов.
4. Цены — ориентир по открытым прайсам Москвы (цены на 21.09.2026), не коммерческое предложение; «по КП» — расценки нет, строка в итог не входит.
5. Демонтаж — по плану демонтажа и общим указаниям: покрытия пола, отделка стен и потолков, дверные блоки — до основания; объёмы справочные — по плану демонтажа (расценки в книге нет — «по КП»).
6. Штробы в стенах — только после технического заключения о несущих стенах (общие указания, план обмера и демонтажа): строка «Штробы в стенах» вертикальные спуски кабеля от потолочной трассы к точкам, объём не меньше фактического (горизонтальные трассы — по исполнительной схеме). Расценки штробления в прайсе нет — «по КП», в итог не входит; кабель в штробах стен прокладывается после неё.
7. Слаботочные сети: кабель по лучам от ЩС** 49,80 м (U/UTP, RG-6, домофон — по видам), гофра 44,80 м, щит ЩС** с патч-панелью; розетки RJ45 и ТВ монтируются в строке «Электроточка». Длины те же, что в ведомости изделий электрика (одна модель — lowcurrent-engineer/bom.js); оборудование заказчика (точки доступа, камеры, коммутатор) в спецификацию не входит.
8. Коробы: стояков (Ш1 — 2,11 м²) и К1 над чистым полом (1,45 м открытых участков; труба К1 вдоль стен 11,22 м в короб не зашивается — она за приборами, в раме инсталляции и в шахтах). В спецификации ВК короб К1 заказывается с запасом 10 % — 1,60 м. Материалы коробов стояков и инсталляции — в спецификации материалов, К1 — в спецификации ВК.

**Допущения и предложения на листе**

Основа листа: размеры сняты с плана заказчика, контрольный обмер не выполнен (К-5); высота потолка 2700 мм принята: на плане заказчика не указана (К-5); подрайон климата не задан — принят не северный (жилые от 2,5 м) (К-4); толщины стен приняты: наружные 250 мм, перегородки 120 мм — не обмерены (К-5); разрешённая мощность 15 кВт принята по типовой квартире, технических условий нет (К-6).

Знак «**» — предложение проектировщика, заказчиком не утверждено (согласовать с заказчиком): ЩС — щит слаботочный: место и состав.

См. лист открытых вопросов (лист 6, записи К-4–К-6).

| Изм. | Кол.уч | Лист | № док. | Подп. | Дата |
|---|---|---|---|---|---|
| Разраб. | | Кырлан А.С. | | | 04.11.26 |
| Пров. | | | | | |
| ГИП | | | | | |
| Н. контр. | | | | | |
| Утв. | | | | | |

**ГД-2026-006-АИ**

Квартира 58 м²

Общая площадь 55,23* м² · * размеры приняты, не замерены (реестр — л. 6, 7, К-5)

Дизайн-проект интерьера

| Стадия | Лист | Листов |
|---|---|---|
| РП | 83 | 87 |

**Ведомость объёмов работ (окончание)**

М б/м

**Кырлан Александр Сергеевич**

выпуск 04.11.2026 № 3da8f16a26 · стр. 92 из 96

# Спецификация материалов

ПРЕДВАРИТЕЛЬНО · не для производства работ · открыто пунктов: 10 (реестр — л. 6, 7)

Отделочные материалы: чистое количество, запас, упаковка, к заказу · ГОСТ 21.110-2013

## Спецификация материалов (ГОСТ 21.110-2013, форма 1)

| Поз. | Наименование и техническая характеристика | Тип, марка, артикул | Код продукции | Поставщик | Ед. изм. | Количество | | | | Масса ед., кг | Примечание |
|---|---|---|---|---|---|---|---|---|---|---|---|
| | | | | | | чистое | запас, % | упаковка | к заказу | | |
| **Покрытия полов и облицовка** | | | | | | | | | | | |
| 1 | Инженерная доска (дуб натуральный, рабочий слой 4 мм, эмиссия E1, прямая укладка) | аналог: инженерная доска, дуб натуральный, масло, 1-полосная, 14/4 мм | | | м² | 41,08 | 7 | по артикулу | 44,00 м² | | пом. 1, 2, 6; до целой упаковки; л. 47, 48 |
| 2 | Клей для паркетной и инженерной доски (эластичный, по ТУ изготовителя доски) | по выбору подрядчика | | | м² | 41,08 | | ведро по ТУ | по ТУ | | расход кг/м² — по ТУ клея; л. 47 |
| 3 | Керамогранит 600×600 мм SG651622R | SG651622R | | | шт | 48 | 10 | коробка | 54 шт | | 12 целых + 36 с подрезкой; 14,30 м² по раскладке, к заказу 19,44 м²; пом. 3, 4, 5; л. 43–46 |
| 4 | Керамогранит 1200×600 мм 610015000370 | 610015000370 | | | шт | 87 | 10 | коробка | 98 шт | | 0 целых + 87 с подрезкой; 31,81 м² по раскладке, к заказу 70,56 м²; пом. 3, 4; л. 43–46 |
| **Сухие смеси и гидроизоляция** | | | | | | | | | | | |
| 5 | Клей плиточный цементный класса C2 S1 (ГОСТ Р 56387-2018) | по выбору подрядчика | | | кг | 31,17 | 10 | мешок 25 кг | 2 меш. | 25 | слой 5 мм, 1,50 кг/м² на 1 мм; л. 43 |
| 6 | Клей плиточный цементный класса C2 (ГОСТ Р 56387-2018) | по выбору подрядчика | | | кг | 301,17 | 10 | мешок 25 кг | 14 меш. | 25 | слой 5 мм, 1,50 кг/м² на 1 мм; л. 43 |
| 7 | Затирка цементная класса класс не задан, цвет — по колерной карте | по выбору подрядчика | | | кг | 3,51 | 10 | упак. 2 кг | 2 упак. | 2 | расход (a+b)/ab × шов × t × 1,6 кг/м²; л. 43 |
| 8 | Гидроизоляция обмазочная полимерная, 2 слоя, лента в углах, манжеты на выводах | по выбору подрядчика | | | м² | 7,07 | 10 | ведро по ТУ | по ТУ | | пом. 3, 4; расход кг/м² — по ТУ; л. 43 |
| 9 | Лента демпферная по периметру пола из плитки | по выбору подрядчика | | | м | 19,14 | 10 | рулон | 22,00 м | | л. 43 |
| 10 | Смесь цементно-песчаная для стяжки М200 (50 мм, 33 мм) | по выбору подрядчика | | | м³ | 2,71 | 5 | мешок по ТУ | по ТУ | | S 55,81 м² × толщина; армирование и маяки — по ТУ; л. 47 |
| 11 | Смесь штукатурная гипсовая для машинного и ручного нанесения по маякам, слой до 10 мм | по выбору подрядчика | | | м² | 24,67 | 10 | мешок по ТУ | по ТУ | | пом. 6; расход кг/м² на 1 мм слоя — по ТУ смеси, толщина — по замеру кривизны стен; л. 14, 48 |
| **Короба из ГКЛВ** | | | | | | | | | | | |
| 12 | Лист ГКЛВ 12,5 мм, 2500 × 1200 мм, обшивка коробов в 2 слоя | по выбору подрядчика | | | м² | 4,22 | 10 | лист 3,00 м² | 2,00 лист | | короб Ш1 пом. 3: 2,11 м²; площадь × 2 слоя; короб К1 над полом — в спецификации ВК; л. 29, 43–46 |
| 13 | Профиль стальной оцинкованный 27 × 28 мм: каркас коробов (стойки и направляющие) | по выбору подрядчика | | | м | 12,08 | 10 | хлыст 3 м | 5 шт | | стойки через 400 мм по свободному периметру + направляющие по полу и потолку; крепёж, лента, шпаклёвка швов — по узлу короба; л. 29, 43–46 |
| **Слаботочные сети** | | | | | | | | | | | |
| 14 | Кабель домофона — тип по системе поставщика | по выбору подрядчика | | | м | 3,40 | | бухта по ТУ | 4,00 м | | по лучам от ЩС**, 1 точ., запас 10 % уже в длине; л. 26 |
| 15 | Кабель коаксиальный RG-6 (75 Ом) к розеткам ТВ | по выбору подрядчика | | | м | 16,30 | | бухта по ТУ | 17,00 м | | по лучам от ЩС**, 1 точ., запас 10 % уже в длине; л. 26 |
| 16 | Кабель U/UTP кат. 5e (LAN, Wi-Fi и камеры по PoE) | по выбору подрядчика | | | м | 30,10 | | бухта по ТУ | 31,00 м | | по лучам от ЩС**, 2 точ., запас 10 % уже в длине; л. 26 |
| 17 | Гофротруба Ø20 для слаботочных линий, отдельно от силовых | по выбору подрядчика | | | м | 44,80 | | бухта по ТУ | 45,00 м | | по длине лучей без участков в канале плинтуса (≈ 90 %); л. 26 |
| 18 | Розетка компьютерная RJ45, кат. 6, с рамкой и подрозетником | по выбору подрядчика | | | шт | 2 | | шт | 2 шт | | LAN1, LAN2; серия механизмов — как у розеток и выключателей; л. 23, 26 |

**Допущения и предложения на листе**

Основа листа: размеры сняты с плана заказчика, контрольный обмер не выполнен (К-5); высота потолка 2700 мм принята: на плане заказчика не указана (К-5); подрайон климата не задан — принят не северный (жилые от 2,5 м) (К-4); толщины стен приняты: наружные 250 мм, перегородки 120 мм — не обмерены (К-5); разрешённая мощность 15 кВт принята по типовой квартире, технических условий нет (К-6).

Знак «**» — предложение проектировщика, заказчиком не утверждено (согласовать с заказчиком): ЩС — щит слаботочный: место и состав; пол пом. 1, 2, 6 — артикул изделия не выбран: позиция описана характеристиками («аналог по характеристикам»), артикул выбирается при закупке.

См. лист открытых вопросов (лист 6, записи К-4–К-6).

| Изм. | Кол.уч | Лист | № док. | Подп. | Дата |
|---|---|---|---|---|---|
| Разраб. | | Кырлан А.С. | | | 04.11.26 |
| Пров. | | | | | |
| ГИП | | | | | |
| | | | | | |
| Н. контр. | | | | | |
| Утв. | | | | | |

**ГД-2026-006-АИ**

Квартира 58 м²

Общая площадь 55,23* м² · * размеры приняты, не замерены (реестр — л. 6, 7, К-5)

Дизайн-проект интерьера

| Стадия | Лист | Листов |
|---|---|---|
| РП | 84 | 87 |

**Спецификация материалов**

М б/м

**Кырлан Александр Сергеевич**

# Спецификация материалов (окончание)

ПРЕДВАРИТЕЛЬНО · не для производства работ · открыто пунктов: 10 (реестр — л. 6, 7)

Отделочные материалы: чистое количество, запас, упаковка, к заказу · ГОСТ 21.110-2013

## Спецификация материалов (ГОСТ 21.110-2013, форма 1) (продолжение)

| Поз. | Наименование и техническая характеристика | Тип, марка, артикул | Код продукции | Поставщик | Ед. изм. | Количество | | | | Масса ед., кг | Примечание |
|---|---|---|---|---|---|---|---|---|---|---|---|
| | | | | | | чистое | запас, % | упаковка | к заказу | | |
| 19 | Розетка телевизионная (коаксиальная) с рамкой и подрозетником | по выбору подрядчика | | | шт | 1 | | шт | 1 шт | | ТВ1; серия механизмов — как у розеток и выключателей; л. 23, 26 |
| 20 | Трубка или монитор домофона (поставка домофонной организации) | по выбору подрядчика | | | шт | 1 | | шт | 1 шт | | ДФ1; серия механизмов — как у розеток и выключателей; л. 23, 26 |
| 21 | Щит слаботочный ЩС**: корпус, DIN-рейка, розетки 220 В | по выбору подрядчика | | | шт | 1 | | шт | 1 шт | | ЩС**; серия механизмов — как у розеток и выключателей; л. 23, 26 |
| 22 | Патч-панель, портов не менее 2 | по выбору подрядчика | | | шт | 1 | | шт | 1 шт | | серия механизмов — как у розеток и выключателей; л. 23, 26 |
| **Лакокрасочные материалы** | | | | | | | | | | | |
| 23 | Краска интерьерная акриловая, полуматовая, класс истирания 1 | Tikkurila S 1002-Y50R | | | л | 9,90 | 10 | банка 2,7 л | 5 банк | | 41,25 м² × 2 сл. × 0,12 л/м²; пом. 1; л. 48 |
| 24 | Краска интерьерная водно-дисперсионная, глубокоматовая, класс истирания 1 | Tikkurila S 0300-N | | | л | 11,83 | 10 | банка 2,7 л | 5 банк | | 49,29 м² × 2 сл. × 0,12 л/м²; пом. 1 (пот.), 2 (пот.), 3 (пот.), 4 (пот.), 5 (пот.); л. 48 |
| 25 | Краска интерьерная акриловая, глубокоматовая, класс истирания 2 | Tikkurila S 1502-Y50R | | | л | 8,14 | 10 | банка 2,7 л | 4 банк | | 33,91 м² × 2 сл. × 0,12 л/м²; пом. 2; л. 48 |
| 26 | Краска интерьерная акриловая, полуматовая, класс истирания 1 | Tikkurila S 1502-Y50R | | | л | 5,44 | 10 | банка 2,7 л | 3 банк | | 22,66 м² × 2 сл. × 0,12 л/м²; пом. 5; л. 48 |
| 27 | Краска интерьерная акриловая, матовая, класс истирания 1 | Tikkurila Harmony V503 «Winter» | | | л | 5,92 | 10 | банка 2,7 л | 3 банк | | 24,67 м² × 2 сл. × 0,12 л/м²; пом. 6; л. 48 |
| 28 | Краска интерьерная акриловая, глубокоматовая, класс истирания 2 | Tikkurila Anti-Reflex 2 V503 «Winter» | | | л | 1,43 | 10 | банка 2,7 л | 1 банк | | 5,94 м² × 2 сл. × 0,12 л/м²; пом. 6 (пот.); л. 48 |
| 29 | Шпаклёвка финишная полимерная под окраску (стены и потолки, Q3) | по выбору подрядчика | | | м² | 177,72 | 10 | ведро по ТУ | по ТУ | | расход кг/м² на слой — по ТУ; л. 48 |
| 30 | Грунтовка акриловая глубокого проникновения, 2 слоя | по выбору подрядчика | | | м² | 208,78 | 10 | канистра по ТУ | по ТУ | | расход л/м² — по ТУ; л. 48 |
| **Погонажные изделия и потолки** | | | | | | | | | | | |
| 31 | Плинтус напольный МДФ под покраску, h=110 мм, крепление к стене | SX184 | | | м.п. | 48,82 | 10 | хлыст 2,4 м | 23 шт | | пом. 1, 2, 5, 6; длина хлыста — по артикулу; л. 48 |
| 32 | Потолок подвесной ГКЛ/ГКЛВ по каркасу Knauf П113: листы, профили, подвесы, лента, шпаклёвка швов | Knauf П113 | | | м² | 49,29 | | комплект | по л. потолков | | площадь — по ведомости потолков; число листов, профилей и подвесов — по шагам каркаса на листе потолков; л. 40–42 |

## Примечания

1. Чистое количество — из ведомости объёмов работ и раскладки плитки; запас — отдельной графой (доска — по ведомости отделки, плитка, краска и плинтус — 10 %); «к заказу» — с запасом и кратно упаковке.
2. Плитка — штуками по раскладке, запас на каждую поверхность. Калибр (рабочий размер) и тон — одной партией на помещение, калибр указать при заказе и сверить с раскладкой до укладки.
3. Краска — 0,12 л/м² на слой (середина вилки 0,10–0,15 л/м²) по фактической площади окраски из ведомости отделки; колеровка одной партией.
4. «По ТУ» — расход задаёт производитель выбранного продукта; количество к заказу — после выбора марки.
5. Поз. 1 заданы характеристиками («аналог:»): марку, артикул и поставщика согласовать с заказчиком до закупки, без артикула не заказывать.
6. Штукатурная смесь — на ту же площадь, что строка ВОР «Штукатурка стен» (24,67 м²): площадь одна, расход смеси задаёт производитель.
7. Коробы инсталляции и стояков: ГКЛВ в 2 слоя и профиль 27 × 28 мм считаются по свободным граням коробов (источник — раскладка плиточника и шахты в данных); короб К1 над полом — в спецификации ВК.
8. Потолки ГКЛ: в этой спецификации — площадь системы П113; число листов, профилей и подвесов — по шагам каркаса на листе потолков (подвесы через 1000, несущие через 500, основные через 1200 мм), схема каркаса не выпущена. Сантехника, светильники и мебель — по своим спецификациям.

**Допущения и предложения на листе**

Основа листа: размеры сняты с плана заказчика, контрольный обмер не выполнен (К-5); высота потолка 2700 мм принята: на плане заказчика не указана (К-5); подрайон климата не задан — принят не северный (жилые от 2,5 м) (К-4); толщины стен приняты: наружные 250 мм, перегородки 120 мм — не обмерены (К-5); разрешённая мощность 15 кВт принята по типовой квартире, технических условий нет (К-6).

Знак «**» — предложение проектировщика, заказчиком не утверждено (согласовать с заказчиком): ЩС — щит слаботочный: место и состав; пол пом. 1, 2, 6 — артикул изделия не выбран: позиция описана характеристиками («аналог по характеристикам»), артикул выбирается при закупке.

См. лист открытых вопросов (лист 6, записи К-4–К-6).

| Изм. | Кол.уч | Лист | № док. | Подп. | Дата |
|---|---|---|---|---|---|
| Разраб. | | Кырлан А.С. | | | 04.11.26 |
| Пров. | | | | | |
| ГИП | | | | | |
| | | | | | |
| Н. контр. | | | | | |
| Утв. | | | | | |

**ГД-2026-006-АИ**

Квартира 58 м²

Общая площадь 55,23* м² · * размеры приняты, не замерены (реестр — л. 6, 7, К-5)

| Дизайн-проект интерьера | Стадия | Лист | Листов |
|---|---|---|---|
| | РП | 85 | 87 |
| **Спецификация материалов (окончание)** М б/м | **Кырлан Александр Сергеевич** | | |

# Смета ориентировочная

**ПРЕДВАРИТЕЛЬНО · не для производства работ · открыто пунктов: 10 (реестр — л. 6, 7)**

Работы, материалы, оборудование, услуги и резерв · цены — ориентир по открытым прайсам, не коммерческое предложение

## Сводная смета (цены на 21.09.2026, Москва)

| № | Наименование работ, материалов, услуг | Ед. изм. | Кол-во | Цена за ед., ₽ | Стоимость, ₽ | | | Чей подряд | Срок поставки, дн. | Основание | Источник цены |
|---|---|---|---|---|---|---|---|---|---|---|---|
| | | | | | план | факт | разница | | | | |
| **Работы — по ведомости объёмов работ** | | | | | | | | | | | |
| 1 | Демонтаж и черновые работы (без 5 поз. по КП) | раздел | 1 | | 121 170 | | | бригада | | ВОР, поз. 1–10; л. 81–83 | по ВОР |
| 2 | Инженерные системы (без 12 поз. по КП) | раздел | 1 | | 69 994 | | | бригада | | ВОР, поз. 11–32; л. 81–83 | по ВОР |
| 3 | Чистовые работы (без 1 поз. по КП) | раздел | 1 | | 459 078 | | | бригада, поставщик | | ВОР, поз. 33–49; л. 81–83 | по ВОР |
| **Материалы — по спецификации материалов** | | | | | | | | | | | |
| 4 | Инженерная доска | м² | 44,00 | 4 513 | 198 572 | | | поставщик | | спецификация, поз. 1 | Ц7 |
| 5 | Керамогранит 600×600 мм | м² | 19,44 | 1 800 | 34 992 | | | поставщик | | спецификация, поз. 3 | Ц6 |
| 6 | Керамогранит 1200×600 мм | м² | 70,56 | 3 500 | 246 960 | | | поставщик | | спецификация, поз. 4 | Ц6 |
| 7 | Клей плиточный цементный класса C2 S1 | меш. | 16 | 1 800 | 28 800 | | | поставщик | | спецификация, поз. 5, 6 | Ц7 |
| 8 | Краска Tikkurila (Harmony, Anti-Reflex 2), банка 2,7 л | банк | 21 | 3 510 | 73 710 | | | поставщик | | спецификация, поз. 23, 24, 25, 26, 27, 28 | Ц6 |
| 9 | Плинтус напольный МДФ под покраску | шт | 23 | 368 | 8 464 | | | поставщик | | спецификация, поз. 31 | Ц7 |
| 10 | Прочие материалы с расходом по ТУ (клей для доски, затирка, гидроизоляция, демпферная лента, смесь для стяжки, смесь штукатурная гипсовая для машинного и ручного нанесения по маякам, лист гклв 12, профиль стальной оцинкованный 27 × 28 мм: каркас коробов (стойки и направляющие), кабель слаботочки, гофра слаботочки, изделия слаботочки, шпаклёвка, грунтовка, каркас и ГКЛ потолков) | компл | 1 | по КП | | | | поставщик | | спецификация, поз. 2, 7, 8, 9, 10, 11, 12, 13, 14, 15, 16, 17, 18, 19, 20, 21, 22, 29, 30, 32 | |
| **Оборудование и мебель — поставка по спецификациям** | | | | | | | | | | | |
| 11 | Кухонный гарнитур по проекту кухни, изготовление и монтаж (4–8 нед.) | компл | 1 | по КП | | | | поставщик | не задан; ориентир 4–8 нед. от замера | л. 55, 56 | |
| 12 | Двери скрытого монтажа с коробом под покраску, поставка | шт | 5 | по КП | | | | поставщик | не задан; ориентир ≈ 30 дн. | л. 16 | |

**Допущения и предложения на листе**

Основа листа: размеры сняты с плана заказчика, контрольный обмер не выполнен (К-5); высота потолка 2700 мм принята: на плане заказчика не указана (К-5); подрайон климата не задан — принят не северный (жилые от 2,5 м) (К-4); толщины стен приняты: наружные 250 мм, перегородки 120 мм — не обмерены (К-5); разрешённая мощность 15 кВт принята по типовой квартире, технических условий нет (К-6).

См. лист открытых вопросов (лист 6, записи К-4–К-6).

| Изм. | Кол.уч | Лист | № док. | Подп. | Дата |
|---|---|---|---|---|---|
| Разраб. | | Кырлан А.С. | | | 04.11.26 |
| Пров. | | | | | |
| ГИП | | | | | |
| | | | | | |
| Н. контр. | | | | | |
| Утв. | | | | | |

**ГД-2026-006-АИ**

Квартира 58 м²

Общая площадь 55,23* м² · * размеры приняты, не замерены (реестр — л. 6, 7, К-5)

Дизайн-проект интерьера

| Стадия | Лист | Листов |
|---|---|---|
| РП | 86 | 87 |

**Смета ориентировочная**

М б/м

**Кырлан Александр Сергеевич**

# Смета ориентировочная (окончание)

ПРЕДВАРИТЕЛЬНО · не для производства работ · открыто пунктов: 10 (реестр — л. 6, 7)

Работы, материалы, оборудование, услуги и резерв · цены — ориентир по открытым прайсам, не коммерческое предложение

## Сводная смета (цены на 21.09.2026, Москва) (продолжение)

| № | Наименование работ, материалов, услуг | Ед. изм. | Кол-во | Цена за ед., ₽ | Стоимость, ₽ | | | Чей подряд | Срок поставки, дн. | Основание | Источник цены |
|---|---|---|---|---|---|---|---|---|---|---|---|
| | | | | | план | факт | разница | | | | |
| 13 | Оборудование заказчика слаботочных сетей: коммутатор — 1 шт | компл | 1 | по КП | | | | заказчик | | л. 23 | |
| 14 | Сантехника, светильники, мебель и предметы интерьера | компл | 1 | по КП | | | | поставщик | | л. 38; л. 39; л. 58; л. 19 | |
| **Прочие работы и услуги** | | | | | | | | | | | |
| 15 | Вынос и вывоз строительного мусора | м³ | | по факту | | | | бригада | | после демонтажа | |
| 16 | Подъём материалов на этаж (лифтом или вручную — по договору) | т | | по факту | | | | бригада | | по массе поставки | |
| 17 | Доставка чистовых материалов, 10 % от поставки | | | 10 % | 59 150 | | | поставщик | | от суммы материалов | |
| 18 | Уборка после ремонта | м² | 55,23 | по факту | | | | бригада | | S квартиры | |
| | **Итого работы** | | | | **650 242** | | | | | | |
| | **Итого материалы** | | | | **591 498** | | | | | | |
| | **Итого прочие услуги** | | | | **59 150** | | | | | | |
| | **Резерв на непредвиденные работы и материалы, 15 %** | | | | **195 134** | | | | | | |
| | **ВСЕГО ориентировочно (без оборудования и позиций по КП)** | | | | **1 496 024** | | | | | | |

## Примечания

1. Смета ориентировочная, не коммерческое предложение: объёмы — из ведомости объёмов работ и спецификации материалов, цены — нижняя граница открытых прайсов Москвы (цены на 21.09.2026); перед договором цены подтвердить у подрядчика и поставщиков.
2. Источники цен: Ц1 — Домашний мастерок: прайс на отделочные работы, 2026; Ц2 — Домашний мастерок: прайс на плиточные работы, 2026; Ц3 Домашний мастерок: прайс на электромонтажные работы, 2026; Ц4 — Профи ремонтник: штукатурно-малярные работы; Ц5 — Profi.ru: укладка керамогранита на стены, Москва 2026; Ц6 — knowledge/spec-materials.md, разд. 1 и 3: ориентир по сегментам; Ц7 — Розница Москвы, 09.2026: Лемана ПРО, KGSnab, официальный дилер Farrow & Ball.
3. В итог не вошли позиции «по КП» и «по факту»: оборудование и мебель, двери, материалы с расходом по ТУ, вывоз мусора, подъём и уборка.
4. Доставка — 10 % от материалов, резерв — 15 % (частный ремонт 10–20 %) отдельными строками, в количествах не спрятаны. Графы «факт» и «разница» заполняются по актам.

**Допущения и предложения на листе**

Основа листа: размеры сняты с плана заказчика, контрольный обмер не выполнен (К-5); высота потолка 2700 мм принята: на плане заказчика не указана (К-5); подрайон климата не задан — принят не северный (жилые от 2,5 м) (К-4); толщины стен приняты: наружные 250 мм, перегородки 120 мм — не обмерены (К-5); разрешённая мощность 15 кВт принята по типовой квартире, технических условий нет (К-6).

См. лист открытых вопросов (лист 6, записи К-4–К-6).

| Изм. | Кол.уч | Лист | № док. | Подп. | Дата |
|---|---|---|---|---|---|
| Разраб. | | Кырлан А.С. | | | 04.11.26 |
| Пров. | | | | | |
| ГИП | | | | | |
| | | | | | |
| Н. контр. | | | | | |
| Утв. | | | | | |

**ГД-2026-006-АИ**

Квартира 58 м²

Общая площадь 55,23* м² · * размеры приняты, не замерены (реестр — л. 6, 7, К-5)

Дизайн-проект интерьера

| Стадия | Лист | Листов |
|---|---|---|
| РП | 87 | 87 |

**Смета ориентировочная (окончание)**

М б/м

**Кырлан Александр Сергеевич**