L

LINEA

ДИЗАЙН-ПРОЕКТ ИНТЕРЬЕРА

Квартира с кабинетом

современный модерн



ПАЛИТРА ОТДЕЛКИ

F&B No. 15	V503	F&B No. 34	NCS S 2010-Y30	NCS S 5020-G50
49 %	41 %	9 %	текстиль, декор	текстиль, декор

АВТОР ПРОЕКТА

Кырлан Александр Сергеевич

Ноябрь 2026



Визуализация гостиной · 3D

ОБЩАЯ ПЛОЩАДЬ	ПОМЕЩЕНИЙ	СТАДИЯ	ШИФР	ОСНОВА
127,29 м²	9, из них жилых 4	Рабочий проект · предварительно	ГД-2026-008-АИ	план заказчика, без обмера

Изм.	Кол.уч	Лист	№ док.	Подп.	Дата	ГД-2026-008-АИ		
						Квартира с кабинетом		
						Общая площадь 127,29* м² · * размеры со скана, не замерены (реестр — л. 6–8, К-1)		
Разраб.		Кырлан А.С.			04.11.26	Дизайн-проект интерьера	Стадия: РП	Лист: 1 / Листов: 131
Пров.						Титульный лист	Кырлан Александр Сергеевич	
ГИП						М б/м		
Н. контр.								
Утв.								

выпуск 04.11.2026 № 4177cbe7a3 · стр. 1 из 166

Общие данные

ПРЕДВАРИТЕЛЬНО · не для производства работ · открыто пунктов: 13 (реестр — л. 6–8)

Комплект ГД-2026-008-АИ · Квартира с кабинетом · современный модерн

Допущения и предложения на листе. См. лист открытых вопросов (листы 6–8).

Ведомость рабочих чертежей основного комплекта ГД-2026-008-АИ

Лист	Наименование	Примечание
1	Титульный лист	
2	Общие данные	
3	Общие данные	
4	Общие данные	
5	Общие данные	
6	Открытые вопросы, принятые допущения и конфликты. Лист 1 из 3	
7	Открытые вопросы, принятые допущения и конфликты. Лист 2 из 3	
8	Открытые вопросы, принятые допущения и конфликты. Лист 3 из 3	
9	Задание на контрольный обмер и обследование. Лист 1 из 3	
10	Задание на контрольный обмер и обследование. Лист 2 из 3	
11	Задание на контрольный обмер и обследование. Лист 3 из 3	
12	График закупок и работ. Лист 1 из 3	
13	График закупок и работ. Лист 2 из 3	
14	График закупок и работ. Лист 3 из 3	
15	Обмерный план	
16	План демонтажа и монтажа перегородок	
17	План дверей	
18	Ведомость заполнения проёмов	
19	Концепция интерьера	
20	План расстановки мебели	
21	Спецификация мебели и оборудования	
22	Спецификация мебели и оборудования (продолжение)	
23	Спецификация мебели и оборудования (продолжение)	
24	Спецификация мебели и оборудования (продолжение)	
25	План розеток и электровыводов	
26	План освещения	
27	План выключателей и схема включения	
28	Ведомость электроточек и изделий	
29	Ведомость электроточек и изделий (продолжение)	
30	Однолинейная схема щита	

Ведомость рабочих чертежей основного комплекта ГД-2026-008-АИ (продолжение)

Лист	Наименование	Примечание
31	Однолинейная схема щита (продолжение)	
32	План принципиальных трасс	
33	План слаботочных сетей	
34	План вентиляции	
35	План отопления	
36	План выводов сантехники	
37	Схема разводки водопровода и канализации	
38	Аксонометрическая схема В1 (холодное водоснабжение)	
39	Аксонометрическая схема Т3 (горячее водоснабжение)	
40	Аксонометрическая схема К1 (канализация)	
41	Развёртки мокрых зон: выводы ВК. Кухня-гостиная	
42	Развёртки мокрых зон: выводы ВК. Ванная (лист 1 из 2)	
43	Развёртки мокрых зон: выводы ВК. Ванная (лист 2 из 2)	
44	Развёртки мокрых зон: выводы ВК. Санузел гостевой (лист 1 из 2)	
45	Развёртки мокрых зон: выводы ВК. Санузел гостевой (лист 2 из 2)	
46	Спецификация сантехнического оборудования	
47	Техническое задание на подбор светильников	
48	План потолков	
49	Разрезы и узлы потолков	
50	Разрезы и узлы потолков (продолжение)	
51	Разрезы и узлы потолков (продолжение)	
52	Сечения потолков М 1:10	
53	Сечения потолков М 1:10	

Общие указания — лист 5: ±0,000 — чистый пол; несущие конструкции и сети дома — по отдельному проекту; скрытые работы — по актам. Открытые вопросы и допущения — листы 6–8.

Изм.	Кол.уч	Лист	№ док.	Подп.	Дата
Разраб.		Кырлан А.С.			04.11.26
Пров.					
ГИП					
Н. контр.					
Утв.					

ГД-2026-008-АИ

Квартира с кабинетом

Общая площадь 127,29* м² · * размеры со скана, не замерены (реестр — л. 6–8, К-1)

Дизайн-проект интерьера

Стадия	Лист	Листов
РП	2	131

Общие данные

М б/м

Кырлан Александр Сергеевич

выпуск 04.11.2026 № 4177cbe7a3 · стр. 2 из 166

Общие данные

Комплект ГД-2026-008-АИ · лист 2 общих данных (продолжение)

Допущения и предложения на листе. См. лист открытых вопросов (листы 6–8).

Ведомость рабочих чертежей основного комплекта ГД-2026-008-АИ (продолжение)

Лист	Наименование	Примечание
54	Раскладка плитки. Планы полов	
55	Раскладка плитки. Прихожая. Фартук кухни	
56	Раскладка плитки. Ванная. Развёртки стен	
57	Раскладка плитки. Санузел гостевой. Развёртки стен	
58	План полов	
59	Ведомость отделки помещений. Лист 1 из 2	
60	Ведомость отделки помещений. Лист 2 из 2	
61	Колерная карта	
62	Спецификация отделочных материалов	
63	Концепция декора и визуализации	
64	План текстиля и декора	
65	Шторы и карнизы	
66	Ведомость текстиля	
67	Ведомость декора. Схемы развески	
68	Схемы развески (продолжение)	
69	Встроенная мебель. Схема расположения	
70	Система хранения Г1	
71	Система хранения Г2	
72	Шкаф распашной Кб1	
73	ТВ-стена Кх12	
74	Шкаф распашной Кх13	
75	Шкаф распашной Дт1	
76	Тумба под раковину Вн1	
77	Шкаф-купе Пх1	
78	Кухня (пом. 4). Развёртка гарнитура	
79	Кухня (пом. 4). Монтажная схема	
80	Остров Кх6 (пом. 4). Чертёж изделия	
81	Шкафы. Монтажная схема. Лист 1 из 2	
82	Шкафы. Монтажная схема. Лист 2 из 2	
83	Ведомости изделий, техники и фурнитуры	

Ведомость рабочих чертежей основного комплекта ГД-2026-008-АИ (продолжение)

Лист	Наименование	Примечание
84	Реестр марок отделки и позиций альбома	
85	Схема расположения развёрток и узлов	
86	Развёртка стены А. Спальня (пом. 1)	
87	Развёртка стены Б. Спальня (пом. 1)	
88	Привязки электроточек, стена Б. Спальня (пом. 1)	
89	Развёртка стены В. Спальня (пом. 1)	
90	Развёртка стены Г. Спальня (пом. 1)	
91	Развёртки стен А, Б. Гардеробная-постирочная (пом. 2)	
92	Развёртки стен В, Г. Гардеробная-постирочная (пом. 2)	
93	Развёртка стены А. Кабинет (пом. 3)	
94	Развёртка стены Б. Кабинет (пом. 3)	
95	Развёртка стены В. Кабинет (пом. 3)	
96	Развёртка стены Г. Кабинет (пом. 3)	
97	Развёртка стены Г. Кухня-гостиная (пом. 4), кухонный фронт	
98	Привязки электроточек, стена Г. Кухня-гостиная (пом. 4)	
99	Развёртка стены Г: схема и ведомость отделки. Кухня-гостиная (пом. 4)	
100	Развёртка стены А. Кухня-гостиная (пом. 4), кухонный фронт	
101	Привязки электроточек и выводов ВК, стена А. Кухня-гостиная (пом. 4)	
102	Развёртка стены А: схема и ведомость отделки. Кухня-гостиная (пом. 4)	
103	Развёртка стены Б. Кухня-гостиная (пом. 4)	
104	Привязки электроточек, стена Б. Кухня-гостиная (пом. 4)	
105	Развёртка стены Б: схема и ведомость отделки. Кухня-гостиная (пом. 4)	
106	Развёртка стены В. Кухня-гостиная (пом. 4)	

Общие указания — лист 5: ±0,000 — чистый пол; несущие конструкции и сети дома — по отдельному проекту; скрытые работы — по актам. Открытые вопросы и допущения — листы 6–8.

Изм.	Кол.уч	Лист	№ док.	Подп.	Дата
Разраб.		Кырлан А.С.			04.11.26
Пров.					
ГИП					
Н. контр.					
Утв.					

ГД-2026-008-АИ

Квартира с кабинетом

Общая площадь 127,29* м² · * размеры со скана, не замерены (реестр — л. 6–8, К-1)

Дизайн-проект интерьера

Стадия	Лист	Листов
РП	3	131

Общие данные

М б/м

Кырлан Александр Сергеевич

выпуск 04.11.2026 № 4177cbe7a3 · стр. 3 из 166

Общие данные

Комплект ГД-2026-008-АИ · лист 3 общих данных (продолжение)

Ведомость рабочих чертежей основного комплекта ГД-2026-008-АИ (продолжение)

Лист	Наименование	Примечание
107	Развёртка стены В: схема и ведомость отделки. Кухня-гостиная (пом. 4)	
108	Развёртки стен А1, А2. Коридор (пом. 5)	
109	Развёртка стены В. Коридор (пом. 5)	
110	Развёртка стены Г. Коридор (пом. 5)	
111	Развёртки стен А, Б. Детская (пом. 6)	
112	Привязки электроточек, стена Б. Детская (пом. 6)	
113	Развёртка стены В. Детская (пом. 6)	
114	Развёртка стены Г. Детская (пом. 6)	
115	Развёртки стен А, Б. Ванная (пом. 7)	
116	Привязки электроточек и выводов ВК, стена Б. Ванная (пом. 7)	
117	Развёртки стен В, Г. Ванная (пом. 7)	
118	Привязки выводов ВК, стена Г. Ванная (пом. 7)	
119	Развёртка стены Б. Прихожая (пом. 8)	
120	Развёртки стен В, Г. Прихожая (пом. 8)	
121	Развёртки стен А, Б, В. Санузел гостевой (пом. 9)	
122	Привязки электроточек и выводов ВК, стена А. Санузел гостевой (пом. 9)	
123	Развёртка стены Г. Санузел гостевой (пом. 9)	
124	Узлы	
125	Ведомость объёмов работ	
126	Ведомость объёмов работ (продолжение)	
127	Ведомость объёмов работ (окончание)	
128	Спецификация материалов	
129	Спецификация материалов (окончание)	
130	Смета ориентировочная	
131	Смета ориентировочная (окончание)	

Ведомость ссылочных и прилагаемых документов

Обозначение	Наименование	Примечание
	Ссылочные документы	
ГОСТ 21.201-2011	СПДС. Условные графические изображения элементов зданий, сооружений и конструкций	
ГОСТ 21.205-2016	СПДС. Условные обозначения элементов санитарно-технических систем	
ГОСТ 21.210-2014	СПДС. Изображения условные графические электрооборудования и проводок на планах	
ГОСТ 2.306-68	ЕСКД. Обозначения графические материалов и правила их нанесения на чертежах	
	Прилагаемые документы	
ГД-2026-008-АИ.В1	Визуализация. Вид сверху (3D), схематичная модель по плану: мебель, текстиль и декор из данных проекта	альбом визуализаций
ГД-2026-008-АИ.В2	Визуализация. Интерьер: Ванная (пом. 7), стена Б	
ГД-2026-008-АИ.В3	Визуализация. Интерьер: Ванная (пом. 7), стена В	
ГД-2026-008-АИ.В4	Визуализация. Интерьер: Ванная (пом. 7), стена Г	
ГД-2026-008-АИ.В5	Визуализация. Интерьер: Санузел гостевой (пом. 9), стена В	
ГД-2026-008-АИ.В6	Визуализация. Интерьер: Санузел гостевой (пом. 9), общий вид	
ГД-2026-008-АИ.В7	Визуализация. Интерьер: Спальня (пом. 1), стена А	
ГД-2026-008-АИ.В8	Визуализация. Интерьер: Спальня (пом. 1), стена Б	
ГД-2026-008-АИ.В9	Визуализация. Интерьер: Спальня (пом. 1), стена Г	
ГД-2026-008-АИ.В10	Визуализация. Интерьер: Коридор (пом. 5), стена В	
ГД-2026-008-АИ.В11	Визуализация. Интерьер: Прихожая (пом. 8), стена Б	
ГД-2026-008-АИ.В12	Визуализация. Интерьер: Прихожая (пом. 8), стена В	
ГД-2026-008-АИ.В13	Визуализация. Интерьер: Прихожая (пом. 8), стена Г	
ГД-2026-008-АИ.В14	Визуализация. Интерьер: Детская (пом. 6), стена А	
ГД-2026-008-АИ.В15	Визуализация. Интерьер: Детская (пом. 6), стена Б	
ГД-2026-008-АИ.В16	Визуализация. Интерьер: Детская (пом. 6), стена Г	

Допущения и предложения на листе

Основа листа: размеры сняты с растрового плана заказчика с частичными размерами: рисунок не в масштабе, помещения выровнены по подписанным размерам мебели и проходов; контрольный обмер не выполнен (К-1); высота потолка 2700 мм принята: на плане заказчика её нет (К-2); толщины стен 300 / 120 мм приняты по плану заказчика, не замерены (К-1); разрешённая мощность 15 кВт принята по типовым ТУ для квартиры, ТУ заказчиком не переданы (К-4); подрайон климата не задан — принят не северный (жилые от 2,5 м) (К-6). См. лист открытых вопросов (лист 6, записи К-1, К-2, К-4, К-6).

Общие указания — лист 5: ±0,000 — чистый пол; несущие конструкции и сети дома — по отдельному проекту; скрытые работы — по актам. Открытые вопросы и допущения — листы 6–8.

Изм.	Кол.уч	Лист	№ док.	Подп.	Дата
Разраб.		Кырлан А.С.			04.11.26
Пров.					
ГИП					
Н. контр.					
Утв.					

ГД-2026-008-АИ

Квартира с кабинетом

Общая площадь 127,29* м² · * размеры со скана, не замерены (реестр — л. 6–8, К-1)

Дизайн-проект интерьера

Стадия	Лист	Листов
РП	4	131

Общие данные

М б/м

Кырлан Александр Сергеевич

выпуск 04.11.2026 № 4177cbe7a3 · стр. 4 из 166

Общие данные

Комплект ГД-2026-008-АИ · лист 4 общих данных (продолжение)

Ведомость ссылочных и прилагаемых документов (продолжение)

Обозначение	Наименование	Примечание
ГД-2026-008-АИ.В17	Визуализация. Интерьер: Кухня-гостиная (пом. 4), стена А	
ГД-2026-008-АИ.В18	Визуализация. Интерьер: Кухня-гостиная (пом. 4), стена Б	
ГД-2026-008-АИ.В19	Визуализация. Интерьер: Кухня-гостиная (пом. 4), стена В	
ГД-2026-008-АИ.В20	Визуализация. Интерьер: Кухня-гостиная (пом. 4), стена Г	
ГД-2026-008-АИ.В21	Визуализация. Интерьер: Кабинет (пом. 3), стена А	
ГД-2026-008-АИ.В22	Визуализация. Интерьер: Кабинет (пом. 3), стена Б	
ГД-2026-008-АИ.В23	Визуализация. Интерьер: Кабинет (пом. 3), стена Г	
ГД-2026-008-АИ.В24	Визуализация. Интерьер: Гардеробная-постирочная (пом. 2), общий вид	

Состав дизайн-проекта

Раздел	Состав	Листы
Обложка	Дизайн-проект интерьера; Квартира с кабинетом; автор проекта — Кырлан Александр Сергеевич	1 с.
Концепция	Стиль Модерн (ар-нуво) 60 % + Современный (контемпорари) 40 %: концепция интерьера, палитра и материалы (колерная карта — лист 61)	л. 19
Визуализации	24 изобр.: Вид сверху (3D), схематичная модель по плану: мебель, текстиль и декор из данных проекта; Ванная, стена Б; Ванная, стена В; Ванная, стена Г; Санузел гостевой, стена В; Санузел гостевой, общий вид; Спальня, стена А; Спальня, стена Б; Спальня, стена Г; Коридор, стена В; Прихожая, стена Б; Прихожая, стена В; Прихожая, стена Г; Детская, стена А; Детская, стена Б; Детская, стена Г; Кухня-гостиная, стена А; Кухня-гостиная, стена Б; Кухня-гостиная, стена В; Кухня-гостиная, стена Г; Кабинет, стена А; Кабинет, стена Б; Кабинет, стена Г; Гардеробная-постирочная, общий вид	В1–В24
Рабочие чертежи	планы, развёртки, узлы (развёртки и узлы — листы 41–45, 85, 91, 92, 108, 111, 115, 117, 120, 121, 124)	л. 1–131
Спецификации и ведомости	оборудование, изделия, отделка, электроточки	л. 18, 21–24, 28, 29, 46, 59–62, 66, 67, 99, 102, 105, 107, 125–129

Общие указания

1. Рабочие чертежи интерьера разработаны на основании задания на проектирование и обмерного плана (лист 15). Объект: Квартира с кабинетом; автор проекта — Кырлан Александр Сергеевич; общая площадь 127,29 м², жилая 92,29 м², помещений 9.
2. Рабочие чертежи выполнены в соответствии с заданием на проектирование и нормативными документами, перечисленными в п. 4.
3. Открытые вопросы, принятые допущения и конфликты между разделами, не снятые к выпуску комплекта, сведены в таблицы на листах 6–8. До ответа по пункту таблицы показанное на указанном там листе — допущение, а не утверждённое решение: комплект по этим листам предварительный.
4. Нормативные документы, на которые есть ссылки в листах комплекта: ГОСТ Р 21.101-2026; ГОСТ 21.501-2018; ГОСТ 2.302-68; ГОСТ 2.303-68; ГОСТ 2.304-81; ГОСТ 2.307-2011; СП 54.13330.2022; СП 71.13330.2017; СП 73.13330.2016; ПУЭ (7-е изд.), гл. 1.8, 7.1; ГОСТ Р 50571.7.701-2024; СанПиН 1.2.3685-21; ГОСТ 2.702; ГОСТ 2.755; ГОСТ 21.110-2013; ГОСТ 21.601; ГОСТ 13996-2019; ГОСТ 23166-2021; ГОСТ 30244; ГОСТ 31173-2016; ГОСТ 31565-2012; ГОСТ 32414-2013; ГОСТ 32415-2013; ГОСТ Р 56387-2018; СП 29.13330.2011; СП 30.13330.2020; СП 51.13330.2011; СП 131.13330. Документы из ведомости ссылочных документов здесь не повторяются.
5. За отметку ±0,000 принят уровень чистого пола жилых помещений квартиры (относительная отметка; абсолютная — по проекту дома). Отметка чистого пола мокрых помещений — −0,015. Размеры — в миллиметрах, отметки — в метрах, площади — в м²; высоты установки H от чистого пола своего помещения до оси изделия.
6. Несущие конструкции, общедомовые стояки, вентиляционные каналы и инженерные сети дома настоящим комплектом не изменяются. Работы, затрагивающие их (проём или штраба в несущей стене, перенос стояка, врезка в вентканал, расширение мокрой зоны), выполняются только по отдельному проекту, к которому прилагается техническое заключение о допустимости и безопасности работ, выданное автором проекта дома или организацией с допуском на обследование, и который согласован в установленном порядке (Жилищный кодекс РФ, ст. 25–29).
7. Трассы инженерных сетей на листах — принципиальные. Расчёты электрических нагрузок и токов КЗ, гидравлики, воздухообмена, освещённости и нагрузок на перекрытие выполняются в проектах ЭОМ, ВК, ОВ и КР организацией с допуском СРО; фактические трассы до закрытия отделкой фиксируются исполнительными схемами.
8. Стиль интерьера — Модерн (ар-нуво) 60 % + Современный (контемпорари) 40 %. Палитра проекта: основной 60 % — Farrow & Ball No. 15 «Bone — мягкий каменно-серый с зеленцой», Tikkurila V503 «Winter»; дополнительный 30 % — Farrow & Ball No. 34 «Calke Green традиционный шалфей», Farrow & Ball No. 286 «Peignoir — серо-розовый»; акцент 10 % — NCS S 5030-B10G «Павлиний сине-зелёный», Farrow & Ball No. 66 «India Yellow — глубокая горчица», NCS S 8010-Y30R «Тёмно-коричневый». Коды цвета — по веерам производителей; цвет утверждается по выкрасу на объекте при освещении проекта.
9. Площади поверхностей — по чистым граням стен до отделки: стены = периметр × высоту от чистого пола помещения до низа потолка минус проёмы (облицовка плиткой — до верха облицовки); плинтус = периметр минус дверные проёмы; пол и потолок — по площади помещения. Количество плиток — по раскладке. Способ один для всех листов комплекта (ведомость отделки, колерная карта, раскладка плитки, развёртки).
10. Марки: стены помещения на всех листах — А (верхняя по плану), Б (правая), В (нижняя), Г (левая); марка отделки О — одна на весь альбом; реестр марок отделки (с позициями колерной карты той же отделки) и марки позиций по видам — на листе 84.
11. Развёртки стен выполнены по всем помещениям для стен с электроточками, мебелью, декором и отделкой: санузлы и кухонный фронт — в М 1:25, остальные стены — в М 1:25; расположение развёрток и узлов — на листе 85, узлы — на листе 124.
12. Перечень скрытых работ, на которые составляются акты освидетельствования (форма по приказу Минстроя России № 344/пр): гидроизоляция пола и стен мокрых помещений (с тестом проливом); стяжка пола (толщина, прочность, влажность основания); скрытая электропроводка (за потолком и в штробах стен; условия штробления — в следующем пункте); трубопроводы водоснабжения и канализации до закрытия (опрессовка, уклоны); закладные и усиления под подвесные приборы, мебель и тяжёлый декор, рамы инсталляций; короба дверей скрытого монтажа до штукатурки; каркасы ГКЛ потолков, коробов и перегородок до обшивки.
13. Скрытая электропроводка: за потолком и в штробах стен. Штробы в стенах выполняются только после технического заключения о несущих конструкциях; до заключения несущие стены не определены, и все стены считаются несущими; объём штроб — в ведомости объёмов работ, строка «Штробы в стенах» (вертикальные спуски; объём не меньше фактического, горизонтальные трассы — по исполнительной схеме).
14. Критерии приёмки: допуски отделочных покрытий — по СП 71.13330.2017; испытания систем водоснабжения и канализации — по СП 73.13330.2016 до закрытия трасс; приёмо-сдаточные испытания электроустановки — по ПУЭ, гл. 1.8, с протоколом электролаборатории.
15. Осознанные отступления от ГОСТ Р 21.101-2026, принятые в комплекте: номер листа и число листов («Листов») указаны на каждом листе; на масштабных листах в основной надписи указан фактический масштаб и дан контрольный отрезок 1000 мм; развёртки стен выполнены в М 1:25 (ГОСТ 21.507-81 — 1:50…1:500) ради читаемости привязок; размерные числа и марки элементов (Д-1, ОК-1, О6) кеглем 2,5 мм, номера помещений — в кружке Ø 8 мм (канон — 3,5 мм и Ø 12 мм): так насыщенные листы А3 читаются без наложений надписей.
16. Графы «Пров.», «Н. контр.», «Утв.» основной надписи заполняются при согласовании комплекта с заказчиком; до согласования комплект подписывает автор проекта (графа «Разраб.»).

Условные обозначения

- контрольный отрезок 1000 мм натуры: по нему проверяют печать 1:1
- отметка уровня, м: ±0,000 — чистый пол жилых помещений
- А — марка развёртки: буква стены, стрелка — взгляд
- О1 — марка отделки по реестру отделки альбома
- выноска узла: над полкой — узел, под полкой — лист

Допущения и предложения на листе

Основа листа: размеры сняты с растрового плана заказчика с частичными размерами: рисунок не в масштабе, помещения выровнены по подписанным размерам мебели и проходов; контрольный обмер не выполнен (К-1); высота потолка 2700 мм принята: на плане заказчика её нет (К-2); толщины стен 300 / 120 мм приняты по плану заказчика, не замерены (К-1); разрешённая мощность 15 кВт принята по типовым ТУ для квартиры, ТУ заказчиком не переданы (К-4); подрайон климата не задан — принят не северный (жилые от 2,5 м) (К-6).

См. лист открытых вопросов (лист 6, записи К-1, К-2, К-4, К-6).

Изм.	Кол.уч	Лист	№ док.	Подп.	Дата
Разраб.		Кырлан А.С.			04.11.26
Пров.					
ГИП					
Н. контр.					
Утв.					

ГД-2026-008-АИ

Квартира с кабинетом

Общая площадь 127,29* м² · * размеры со скана, не замерены (реестр — л. 6–8, К-1)

Дизайн-проект интерьера	Стадия	Лист	Листов
	РП	5	131

Общие данные

М б/м

Кырлан Александр Сергеевич

выпуск 04.11.2026 № 4177cbe7a3 · стр. 5 из 166

Открытые вопросы, принятые допущения и конфликты. Лист 1 из 3

ПРЕДВАРИТЕЛЬНО · не для производства работ · открыто пунктов: 13 (реестр — л. 6–8)

Сводка по реестрам координации (стартовое совещание 18.10.2026)

Комплект предварительный по пунктам этих таблиц. Пока по пункту нет ответа или решения, показанное на указанном листе — допущение проектировщика, а не утверждённое решение.
Сводка: открытых вопросов — 13 (из них ждут факта объекта — 4: контрольного обмера, обследования или документа); изменений в реестре — 9.
Пункты, ответ на которые лежит на объекте, а не за столом проектировщика (графа «Вид», строка «Ждёт»), собраны на листе «Задание на контрольный обмер и обследование» (листы 9–11): что и где замерить, с какой точностью и чем подтвердить. Пункты, ждущие решения человека, на объекте не закрываются.

Открытые вопросы и принятые допущения

№	Формулировка	Вид	Кто решает	Если решения нет	Лист, где это проявляется
К-1	Размеры квартиры сняты с растрового плана заказчика с частичными размерами (рисунок не в масштабе): помещения выровнены по подписанным размерам мебели и проходов. До заказа мебели, дверей и материалов нужен контрольный обмер всех помещений и проёмов.	Отсутствует Ждёт: обмера	Архитектор-планировщик	размеры на листах — по плану заказчика, уточняются по месту; мебель на заказ и материалы по ним не заказывать	л. 15 — Обмерный план л. 20 — План расстановки мебели
К-2	Высота потолка на плане заказчика не указана, принята 2700 мм.	Отсутствует	Архитектор-планировщик	высоты на развёртках и потолки — от 2700 мм, уточнить при обмере	л. 15 — Обмерный план л. 48 — План потолков
К-4	Разрешённая мощность квартиры по ТУ неизвестна, принята 15 кВт.	Отсутствует	Инженер-электрик	щит и группы рассчитаны на 15 кВт; при меньших ТУ пересчёт	л. 30 — Однолинейная схема щита л. 25 — План розеток и электровыводов
К-5	Перепланировка (гардеробная-постирочная при спальне, Г-образный коридор, широкий проём прихожая — гостиная, гостевой санузел у прихожей) — предложение проектировщика: несущие стены дома неизвестны. Нужны поэтажный план БТИ / техзаключение и решение заказчика.	Отсутствует Ждёт: документа	Архитектор-планировщик	перегородки и проёмы — предложение, к строительству не выдаются; мокрые зоны и кухня оставлены на местах плана заказчика	л. 15 — Обмерный план
К-6	Климатический подрайон (СП 131.13330) не задан: принят не северный — жилые комнаты и кухня под потолком от 2,5 м (СП 54, п. 5.12); в IA, IБ, IГ, IД, IVA — от 2,7 м.	Отсутствует Ждёт: документа	Архитектор-планировщик	отметки потолков жилых — по 2,5 м; при северном подрайоне уровни ниже 2,7 м пересчитать до заказа каркаса	л. 48 — План потолков
К-7	Проёмы скрытых дверей Д-2 … Д-7 по плану заказчика высотой 2100 мм, полотно расчётное 2000 мм (ряд UNION FILO-60 Piatto). По каталогам скрытых систем проём под полотно 2000 — 2050–2080 мм, под полотно 2100 — 2150–2180 мм: при проёме 2100 полотно 2000 оставляет над собой лишние 20–50 мм, полотно 2100 не входит. Решить по выбранной модели: проём по высоте 2050–2080 мм под полотно 2000 (как уменьшать — по узлу выбранной модели) или взять полотно 2100 с проёмом 2150–2180 мм (только в ненесущей стене, после контрольного обмера К-1).	Спорно Ждёт: решения	Архитектор-планировщик	проёмы остаются 2100 мм, полотна «расч.» 2000 мм; двери до решения не заказывать	л. 17 — План дверей л. 15 — Обмерный план
К-8	Входная дверь Д-1 (проём 1000 × 2100 мм по плану заказчика): стальной дверной блок не выбран — размер блока и монтажный зазор (ГОСТ 31173-2016) из проёма не выводятся, на листах «блок — задать». Выбрать блок (изготовитель, модель, размер блока, открывание наружу, класс прочности и теплозащиты) и сверить проём по каталогу изготовителя при контрольном обмере (К-1).	Отсутствует Ждёт: решения	Архитектор-планировщик	блок не заказывать, проём не изменять; на листах «блок задать»	л. 17 — План дверей л. 12 — График закупок и работ. Лист 1 из 3
К-10	Душ П10 с трапом (пом. 9, санузел гостевой, по плану заказчика — «душ с трапом и стеклянной перегородкой»): в стяжке 35 мм с облицовкой 14 мм трап не встаёт — монтажная высота трапа ≈ 90 мм от плиты до верха решётки (по паспорту модели) + уклон отвода Ø50 кратчайшим путём вдоль стен до стояка Ст К1-1 (3,11 м × 25 мм/м = 78 мм) = 168 мм при врезке на уровне плиты; врезка выше плиты поднимает подиум на столько же — отметку врезки замерить (К-1). Предложение проектировщика: душевая зона 900 × 1640 у стены В, подиум 120 мм у трапа (решётка +0,105), ступень по открытому краю 127 мм (уклон 15 мм/м к трапу); гидроизоляция по плите под подиумом и по подиуму, весь санузел; отвод от трапа в подиуме — к стене, за краем подиума — в коробе 160×110 вдоль стены до стояка (узел 1 на схеме разводки); смеситель — 1100 мм от пола душа. Расстановкой не решено: край подиума — в 100 мм от проёма Д-7; не помогает: та же зона глубиной 800 — край в 200 мм; зона 900 × 900 в углу В/Г — край в 100 мм. Решить: (а) зона 900 × 900 в углу В/Б — край в 747 мм от проёма, подиум 110 мм у трапа, ступень 117 мм, отвод 2,74 м; у проёма остаётся пол 740 × 900; кадры визуализации санузла перерисовать; (б) проём Д-7 сдвинуть от зоны (решение архитектора, обмер К-1); (в) оставить зону как есть: ступень у проёма осознанно, кромка ступени контрастная, подсветка у пола. Альтернативы по высоте: низкий поддон на ножках (сифон над полом), сверхплоский трап от 70 мм (подиум 100 мм) или подъём пола всего санузла с порогом.	Спорно Ждёт: обмера, затем решения	Инженер ВК (вода, канализация)	трап и подиум не выполнять, пол санузла 9 до решения не стяжать; гидроизоляцию — по листу	л. 36 — План выводов сантехники л. 37 — Схема разводки водопровода и канализации л. 58 — План полов
К-11	Ванна П1 отдельностоящая со смесителем напольным (пом. 7, ванная, по заказчику): подвод ХВ и ГВ к стойке и выпуск Ø50 идут из пола, а стяжка ванной 35 мм их не укрывает — под водопровод Ø20 в полу нужно ≥ 65 мм (Ø + 45, СП 29.13330, п. 8.2), под выпуск Ø50 до стояка Ст К1-2 (3,6 м × 25 мм/м = 90 мм) — ≥ 185 мм. Решить: (а) подъём пола ванной до 185 мм (порог у двери, пересчёт высот выводов и развёрток), (б) смеситель настенный на стене В (выводы ХВ, ГВ на стене) и выпуск ванны к стене открытым сифоном, (в) смеситель на борт ванны. Место стойки на листах — предложение проектировщика.	Спорно Ждёт: решения	Инженер ВК (вода, канализация)	выводы и выпуск ванны П1 не выполнять, ванну и смеситель не заказывать; остальные выводы ванной — по листу	л. 36 — План выводов сантехники л. 37 — Схема разводки водопровода и канализации л. 46 — Спецификация сантехнического оборудования

Изм.	Кол.уч	Лист	№ док.	Подп.	Дата
Разраб.		Кырлан А.С.			04.11.26
Пров.					
ГИП					
Н. контр.					
Утв.					

ГД-2026-008-АИ

Квартира с кабинетом

Общая площадь 127,29* м² · * размеры со скана, не замерены (реестр — л. 6–8, К-1)

Дизайн-проект интерьера

Стадия	Лист	Листов
РП	6	131

Открытые вопросы, принятые допущения и конфликты. Лист 1 из 3
М б/м

Кырлан Александр Сергеевич

выпуск 04.11.2026 № 4177cbe7a3 · стр. 6 из 166

Открытые вопросы, принятые допущения и конфликты. Лист 2 из 3

Сводка по реестрам координации (стартовое совещание 18.10.2026)

Открытые вопросы и принятые допущения (продолжение)

№	Формулировка	Вид	Кто решает	Если решения нет	Лист, где это проявляется
К-12	Проверяющий («Пров.») и нормоконтролёр («Н. контр.») комплекта не назначены: графы штампа пусты на всех листах, данные проекта и данные проекта не заданы. Их заполняет только человек, отличный от разработчика: разработчик подписи за них не ставит. Нужно решение автора — кто проверяет и кто ведёт нормоконтроль (фамилии, разные люди), и дата проверки.	Отсутствует Ждёт: решения	Нормоконтролёр	графы «Пров.» и «Н. контр.» остаются пустыми; комплект предварительный, к производству работ не выдаётся	л. 2 — Общие данные
К-17	Циркуляция ГВС в данных не задана — циркуляционного трубопровода на схеме нет. Решить: нужна ли циркуляция	Отсутствует Ждёт: решения	Инженер ВК (вода, канализация)	циркуляции на схеме нет	л. 41–44 — Развёртки мокрых зон: выводы ВК. Кухня-гостиная л. 38 — Аксонометрическая схема В1 (холодное водоснабжение) л. 37 — Схема разводки водопровода и канализации
К-19	Кухня-гостиная (пом. 4, 45,5 м², два окна): мощность приборов не подтверждена расчётом — РО-5 500×600 (вынесен из модулей, ИЗ-6) и низкий РО-6 1400×200 под банкеткой-экраном (ИЗ-7, теплоотдача за экраном снижается). Нужен теплотехнический расчёт помещения (теплопотери через наружные стены и окна, параметры теплоносителя дома). При нехватке — вертикальный прибор на месте РО-5 или внутрипольный конвектор у окна 2 (решение ОВ).	Отсутствует	Инженер ОВ	РО-5 и РО-6 не заказывать до расчёта; места, подводки и экран — по листам	л. 35 — План отопления
К-20	ТВ-стена Кх12: низ ниши ТВ (+900) — в 150 мм над верхом ниши биокамина (+750). Телевизор и приставка на полке над топкой нагреваются; допустимое расстояние задают паспорта обеих моделей (биокамина — зона нагрева над топкой, телевизора температура эксплуатации). Варианты: (а) выбрать модели и подтвердить расстояние по паспортам; (б) поднять нишу ТВ (низ +1100 и выше — центр экрана выше уровня глаз сидящего); (в) развести ниши по ширине стены (камин сбоку от ТВ). Рекомендация исполнителя — (а), при нехватке расстояния — (б).	Спорно Ждёт: решения	Мебельщик	нишу ТВ не изготавливать до выбора моделей; каркас и облицовку вне ниш — по листу	л. 73 — ТВ-стена Кх12 л. 103 — Развёртка стены Б. Кухня-гостиная (пом. 4)

Изменения проекта после выпуска листов (реестр изменений)

№	Дата	Лист	Было	Стало	Кто решил, подпись
ИЗ-1	26.10.2026	л. 20 — План расстановки мебели л. 21 — Спецификация мебели и оборудования л. 83 — Ведомости изделий, техники и фурнитуры л. 77 — Шкаф-купе Пх1 л. 72 — Шкаф распашной Кб1 л. 64 — План текстиля и декора л. 66 — Ведомость текстиля л. 111 — Развёртки стен А, Б. Детская (пом. 6) л. 67 — Ведомость декора. Схемы развески л. 65 — Шторы и карнизы л. 86 — Развёртка стены А. Спальня (пом. 1)	Шкаф-купе Пх1 описан тремя разными изделиями (зеркальные арки / рифлёные панели / ЛДСП); Кб1 «с арочными фасадами» без арки на чертеже; кровать детской Дт2 на радиаторе РО-9 под окном, ковёр Т22 2500 × 1800 под ней; диван Кх9 «угловой» нарисован прямым; у стола Кх8 6 стульев, три из них — в банкетке Кх7 (за стулом 150 мм). Спальня: шина штор Т1/Т2 одна, 300…2800 по стене А, на окно 1 — пакет штор заходил на окно 2, у окна 2 штор нет.	Предложения проектировщика, заказчиком не утверждены: Пх1 — фасад МДФ 10 мм, эмаль матовая, профиль латунь матовая, зеркальные арочные вставки (поле 100 мм), как на кадре; Кб1 арочная фрезеровка филёнок (поле 100 мм); Дт2 — кровать 800 × 2000 (было 900 × 2000) у стены Б, 1480 мм от угла с дверью: вне радиатора РО-9, от открытого полотна Д-5 620 мм прохода, вдоль кровати к окну 520 мм (кровать 900 между полотном и стеной В не встаёт: 600 + 900 + 500 > 1940 мм); Кх9 — диван угловой Г 2700 × 1600; Кх8 — банкетка Кх7 на 3 места и 3 стула (2 со свободной стороны, 1 у торца). Т22 — ковёр 1200 × 1700 у кресла-кокона Дт4 вместо ковра 2500 × 1800 под кроватью (кровать в 520 мм от стены В: ковёр под ней не выходит за кровать на 450 мм и не оставляет 200 мм пола у стены). До подписи — не заказывать. Знак «**» у Кб1 не ставится: марка Кб1 совпадает с кодом канализации Кб1, и ядро поставило бы знак у каждого «Кб1» на листах ВК; предложение по Кб1 — только в этой записи. Дт2 — изголовье 1000 мм от пола (до выбора модели); ДК2 — низ 1200 мм, на 200 над изголовьем (было 700 от матраса — картина за изголовьем). Спальня: в нише штор по стене А две шины по 2300 мм — Т1/Т2 на окно 1 (0…2300) и Т27/Т28 на окно 2 (2300…4600), верх +2,600 (верх ниши), длину — по обмеру ниши (К-1). Т1, Т2, Т27, Т28 — предложение: на листах со знаком «**», до подписи шины не заказывать.	Утверждено: Кырлан А.С., 01.11.2026. Предложил: исполнитель.
ИЗ-2	30.10.2026	л. 17 — План дверей л. 20 — План расстановки мебели л. 36 — План выводов сантехники л. 27 — План выключателей и схема включения л. 56 — Раскладка плитки. Ванная. Развёртки стен	Ванная (пом. 7): дверь Д-6 (800 мм, стена А, привязка 2300) открывалась внутрь — полотно на 90° задевало тумбу Вн1 (привязка 450) и раковину П2 (привязка 500): дверь не открыть, в выпуске для заказчика — ошибка; П2 стояла в полосе 600 мм перед проёмом. Конфликт Кф-3 открыт.	Проём Д-6 сдвинут вдоль стены А от угла Б: привязка 2300 → 1200 (х 4900…5700), петли у х 4900, открывание внутрь, в сторону стены Г (там полотенцесушитель П7 на стене А 500…1000 — не в секторе). Тумба Вн1, раковины П2, П3, стиральная машина П6 остаются на местах; П2 (500…1100) вне полосы 600 мм перед проёмом. Выключатель S13 в коридоре — к проёму (привязка 3550, со стороны ручки), коробка КУП1 на стене А — привязка 2300. Раскладка плитки стены А пересчитана движком. Знак «**» у Д-6 остаётся до подписи автора; Кф-3 — у владельца до подписи этой записи.	Утверждено: Кырлан А.С., 01.11.2026. Предложил: исполнитель.

Изм.	Кол.уч	Лист	№ док.	Подп.	Дата
Разраб.		Кырлан А.С.			04.11.26
Пров.					
ГИП					
Н. контр.					
Утв.					

ГД-2026-008-АИ

Квартира с кабинетом

Общая площадь 127,29* м² · * размеры со скана, не замерены (реестр — л. 6–8, К-1)

Дизайн-проект интерьера

Стадия	Лист	Листов
РП	7	131

Открытые вопросы, принятые допущения и конфликты. Лист 2 из 3

М б/м

Кырлан Александр Сергеевич

выпуск 04.11.2026 № 4177cbe7a3 · стр. 7 из 166

Открытые вопросы, принятые допущения и конфликты. Лист 3 из 3

Сводка по реестрам координации (стартовое совещание 18.10.2026)

Изменения проекта после выпуска листов (реестр изменений) (продолжение)

№	Дата	Лист	Было	Стало	Кто решил, подпись
ИЗ-3	30.10.2026	л. 20 — План расстановки мебели л. 64 — План текстиля и декора л. 88 — Привязки электроточек, стена Б. Спальня (пом. 1)	Спальня (пом. 1): кресло-ракушка С6 (х 600, у 3000, 750×750) перекрывало туалетный столик С5 (стена В, 500…1700, глубина 450) на 200 мм — на плане кресло поверх столика, на визуализации — рядом; ни одно правило пересечения мебели это не ловило.	С6 переставлено в угол у окна 1 (х 600…1350, у 600…1350), столик С5 свободен; кадры спальни сверить с планом заново (views-check). Знак «**» у С6 до подписи автора.	Утверждено: Кырлан А.С., 01.11.2026. Предложил: исполнитель.
ИЗ-4	30.10.2026	л. 20 — План расстановки мебели л. 21 — Спецификация мебели и оборудования л. 83 — Ведомости изделий, техники и фурнитуры л. 84 — Реестр марок отделки и позиций альбома	Марки мебели кабинета К1–К7 совпадали с позициями колерной карты К1–К8, марки прихожей П8, П9 — с сантехприборами П1–П13: марка неоднозначна в пределах комплекта.	Мебель кабинета — Кб1…Кб7, мебель прихожей — Пх1 (шкаф-купе), Пх2 (банкетка); ссылки точек электрики, текстиля и декора переписаны вместе с марками. Колорист и ВК не тронуты.	Утверждено: Кырлан А.С., 02.11.2026. Предложил: исполнитель.
ИЗ-5	01.11.2026	л. 20 — План расстановки мебели л. 83 — Ведомости изделий, техники и фурнитуры л. 73 — ТВ-стена Кх12 л. 103 — Развёртка стены Б. Кухня-гостиная (пом. 4)	ТВ-стена Кх12 записана 30.10.2026 «автор: Кырлан А.С.» с нишами ТВ 1500×900 (низ +900) и биокамина 900×400 (низ +350) — размеры придумал исполнитель, записи об изменении не было, на листе изделия Д_4 стена рисовалась шкафом с антресолями и штангой (НФ-3, НФ-13 приёмки 01.11.2026).	Предложение исполнителя, заказчиком не утверждено: Кх12 — каркас из оцинкованного профиля на стене Б с облицовкой панелями МДФ 19 мм, эмаль; ниша ТВ 1500×900, низ +900, глубина 400, низ ниши — полка под приставку; ниша биокамина 900×400, низ +350 — облицовка негорючая (сталь 2 мм / камень), зазоры 50 мм до панелей — до паспорта модели (К-13). До подписи — не изготавливать.	Утверждено: Кырлан А.С., 01.11.2026. Предложил: предложение исполнителя по наименованию.
ИЗ-6	01.11.2026	л. 35 — План отопления л. 78 — Кухня (пом. 4). Развёртка гарнитура л. 100 — Развёртка стены А. Кухня-гостиная (пом. 4), кухонный фронт	Радиатор РО-5 выводился листом ОВ под окном 1 кухни (стена А, привязка 1050, 700×600) — внутри модулей Кх3 (посудомоечная машина) и Кх4 (ящики): экран невозможен.	РО-5 — на свободном участке наружной стены А между колонной Кх1 и банкеткой Кх7: привязка 3350, 500×600, низ +120 (х 11750…12250); гарнитур под окном 1 без прибора. Мощность 500-го прибора сверить теплотехническим расчётом ОВ (при нехватке — вертикальный прибор на том же месте); стояки и подводки отопления не замерены (К-1). Все радиаторы квартиры теперь в данных — одни и те же на листе ОВ, в мебели, DXF и IFC.	Утверждено: Кырлан А.С., 01.11.2026. Предложил: исполнитель (ОВ).
ИЗ-7	01.11.2026	л. 35 — План отопления л. 83 — Ведомости изделий, техники и фурнитуры л. 100 — Развёртка стены А. Кухня-гостиная (пом. 4), кухонный фронт	Банкетка Кх7 у окна 2 — экран радиатора РО-6, выведенного листом ОВ 900×600 (низ +120, верх +720): прибор под сиденье банкетки не вставал, низ щита сиденья не задан.	РО-6 — низкий панельный прибор 1400×200 по ширине окна 2 (привязка 4400, низ +120, верх +320); банкетка Кх7: сиденье +450, низ щита сиденья +400 (верх прибора + 80 мм), решётка в лицевой панели, щель 60 мм у стены. Мощность низкого прибора сверить теплотехническим расчётом ОВ (при нехватке — внутрипольный конвектор у окна).	Утверждено: Кырлан А.С., 01.11.2026. Предложил: исполнитель (ОВ, мебель).
ИЗ-8	01.11.2026	л. 80 — Остров Кх6 (пом. 4). Чертёж изделия л. 34 — План вентиляции	Вытяжка над варочной панелью острова Кх6 не была задана (К-9); предложение исполнителя — островная потолочная вытяжка в режиме рециркуляции — ждало решения.	Принято автором (ответ передан координатором): островная потолочная вытяжка 900 мм над Кх6 в режиме рециркуляции (угольный фильтр), низ +1550. Вариант с отводом в вентканал ВК-3 не выбран: короба в потолке нет. После подписи автора вопрос К-9 закрывается, знак предложения снимается. Модель вытяжки не выбрана: крепление к перекрытию и вывод питания на потолке по паспорту модели.	Утверждено: Кырлан А.С., 01.11.2026. Предложил: Александр Кырлан, решение автора.
ИЗ-9	01.11.2026	л. 20 — План расстановки мебели л. 83 — Ведомости изделий, техники и фурнитуры л. 73 — ТВ-стена Кх12 л. 103 — Развёртка стены Б. Кухня-гостиная (пом. 4)	Биокамин в ТВ-стене Кх12: модель, мощность, зазоры и приток не заданы (К-13); до ответа нишу камина изготавливать было нельзя.	Принято автором (ответ передан координатором): биокамин в ТВ-стене Кх12 остаётся, ниша 900×400, низ +350, облицовка негорючая (сталь 2 мм / камень), зазоры 50 мм до панелей. После подписи автора вопрос К-13 «оставлять ли биокамин» закрывается. Модель биокамина не выбрана: зазоры, тепловая мощность и приток воздуха (при мощности > 2 кВт — решение ОВ) уточняются по паспорту модели — пометка на листе остаётся.	Утверждено: Кырлан А.С., 01.11.2026. Предложил: Александр Кырлан, решение автора.

Примечания

1. Номера листов — по ведомости рабочих чертежей комплекта (лист «Общие данные»).
2. Графа «Если решения нет» показывает состояние решения на листах; влияние на сроки и стоимость по пунктам не оценивалось.
3. Пункт, по которому принято решение, при следующем выпуске комплекта из таблиц исключается.

						ГД-2026-008-АИ			
						Квартира с кабинетом Общая площадь 127,29* м² · * размеры со скана, не замерены (реестр — л. 6–8, К-1)			
Изм.	Кол.уч	Лист	№ док.	Подп.	Дата	Дизайн-проект интерьера	Стадия	Лист	Листов
Разраб.		Кырлан А.С.			04.11.26		РП	8	131
Пров.									
ГИП									
						Открытые вопросы, принятые допущения и конфликты. Лист 3 из 3 М б/м		**Кырлан Александр Сергеевич**	
Н. контр.									
Утв.									

ПРЕДВАРИТЕЛЬНО · не для производства работ · открыто пунктов: 13 (реестр — л. 6–8)

Задание на контрольный обмер и обследование. Лист 1 из 3

Что замерить, вскрыть и получить до заказа материалов и изделий

Задание собрано из открытых вопросов, ответ на которые лежит на объекте или в документах, а не за столом проектировщика. Пока факт не получен, размер, материал или положение на листах — допущение (знак «*»), а не замер.
Сводка: на объекте — 10 (до демонтажа — 7; после демонтажа — 2; после черновых работ — 1); документом и при закупке — 3; из допущений в данных и на листах — 10, из них без вопроса в реестре — 5. Закрываются вопросы: К-1, К-2, К-4–К-6, К-10, К-20 (7). Вопросы, ждущие решения человека, задание не закрывает — они решаются по реестру открытых вопросов.

Условия проведения

Порядок работ	Приёмы и точность	Кто присутствует	Если факт не совпал с проектом
1. До демонтажа — существующее состояние: контур, диагонали, высоты, проёмы, оси стояков, ниши и конструкции, которые видны. 2. После демонтажа, до черновых работ — то, что закрывали отделка и короба: основание стен, фактические толщины, углы, узлы. 3. После черновых работ, до чистового пола — габариты кухни и встроенной мебели по готовым стенам: после штукатурки и выравнивания размеры отличаются от размеров до работ. 4. Документы и данные закупки — не на объекте: к сроку из последней таблицы, от них зависят привязки и заказ. Что заказывается по размеру из задания, до закрытия пункта не заказывают: сроки изготовления — по графику закупок прораба.	Обход по часовой стрелке от входа: стены, проёмы, потолок, коммуникации (стояки, щиток, вентканалы), особенности (ниши, короба, выступы). Размеры записывают в мм; сумма участков равна общему размеру, при цепочке длиннее трёх участков ставят проверочный (общий) размер. Диагонали каждого помещения; если две диагонали различаются на 5 мм и больше, разницу подписывают на плане. Потолок — в нескольких точках: центр, углы, у проёмов. Проём — ширина, высота, глубина откоса, привязка к ближайшим углам, высота подоконника. Допустимая погрешность прибора — 2–3 мм на метр; размеры округляют кратно 5 мм; два контрольных промера одного размера не должны расходиться более чем на 2 %. Допуск по пункту — в графе «Точность». План БТИ обмер не заменяет.	Прораб (отвечает за проведение) — назначает день и порядок обхода, открывает объект и освобождает помещения, ведёт это задание и реестр изменений. Архитектор — выполняет обмер, составляет акт контрольного обмера и подписывает результаты по размерам и конструкциям. Владельцы вопросов присутствуют при пунктах своего раздела или принимают результат до заказа: Инженер ВК (вода, канализация) — К-10; позиции О-1; Мебельщик — К-20; Инженер-электрик — К-4; позиции О-2; Инженер ОВ — позиции О-3; Отделочник — позиции О-8, О-9. Заказчик или его представитель — передаёт документы (план БТИ, проект дома, технические условия, паспорта), подписывает акт. Проектных решений на обмере не принимают: обмер даёт факт, решения — по реестру открытых вопросов (листы 6–8).	1. В пределах допуска пункта — принимается измеренное значение, лист перевыпускается, знак «*» снимается. 2. Больше допуска или контрольные промеры расходятся более чем на 2 % — промер повторяют; не подтвердилось — запись в реестр изменений (дата, лист, было, стало, кто решил, подпись), работы в этом месте не начинают. 3. Затронуты несущая стена, стояк, вентканал или мокрая зона — сразу владельцу раздела и ГИПу (главному инженеру проекта); между разделами не больше двух кругов, затем решает ГИП. 4. На объекте устно ничего не согласуется: каждое решение — записью в реестр с подписью.

Этап 1. До демонтажа

№	Где	Способ	Что сделать	Кто выполняет	Точность	Что пересчитается в альбоме	Чем подтверждается	Закрывает вопросы реестра
О-1	Ввод В1 и Т3 у стояков; по всей квартире	Обмер	Отключающая арматура и счётчики воды на вводах: положение, тип, пломбы управляющей компании. Альбом ставит их на каждом вводе по практике, в данных их нет.	Архитектор	±5 мм	Узлы ввода в спецификации ВК (краны, фильтры, счётчики); места ввода на плане выводов. Листы: л. 36 — План выводов сантехники л. 46 — Спецификация сантехнического оборудования	акт контрольного обмера; фото с рулеткой и привязкой к стене или углу	Вопроса в реестре нет: Альбом принимает счётчики воды на вводах без осмотра. Результат принимает: Инженер ВК (вода, канализация)
О-2	Вход в квартиру или лестничная клетка; место щита на плане	Обмер	Существующий щиток и счётчик электроэнергии: место и габарит ниши, состояние ввода, марка и сечение вводного кабеля, наличие вводного автомата и УЗО, пломбы.	Архитектор	±5 мм	Ниша и место щита на листах; вводной кабель и аппараты на однолинейной схеме; расстояния до первых групп. Листы: л. 30, 31 — Однолинейная схема щита	акт контрольного обмера; фото с рулеткой и привязкой к стене или углу	Вопроса в реестре нет: Альбом принимает щит и ввод без осмотра. Результат принимает: Инженер-электрик
О-3	Кухня-гостиная (пом. 4); у окон	Обмер	Положение стояков отопления (подающий и обратный) от граней стен, диаметры, наличие запорной арматуры; существующие радиаторы: число секций, межосевое расстояние, подводки. В данных стояков отопления нет — лист отопления выводит их условно у откоса окна.	Архитектор	±5 мм	План отопления: места стояков и подводок, привязки радиаторов; подбор радиаторов по теплотехническому расчёту; радиаторы и узлы подключения в ВОР и спецификации. Листы: л. 35 — План отопления	акт контрольного обмера; фото с рулеткой и привязкой к стене или углу	Вопроса в реестре нет: Альбом принимает положение стояков и радиаторов отопления без обмера. Результат принимает: Инженер ОВ
О-4	все помещения	Обмер	Контрольный обмер всех помещений: стороны, диагонали, проёмы, высота потолка.	исполнитель	±5 мм; диагонали — разница от 5 мм подписывается	обмерный и монтажный планы, развёртки, мебель на заказ Листы: л. 15 — Обмерный план л. 20 — План расстановки мебели	акт контрольного обмера	К-1 Результат принимает: Архитектор

Допущения и предложения на листе

Основа листа: размеры сняты с растрового плана заказчика с частичными размерами: рисунок не в масштабе, помещения выровнены по подписанным размерам мебели и проходов; контрольный обмер не выполнен (К-1); высота потолка 2700 мм принята: на плане заказчика её нет (К-2); толщины стен 300 / 120 мм приняты по плану заказчика, не замерены (К-1); разрешённая мощность 15 кВт принята по типовым ТУ для квартиры, ТУ заказчиком не переданы (К-4); подрайон климата не задан — принят не северный (жилые от 2,5 м) (К-6).
См. лист открытых вопросов (лист 6, записи К-1, К-2, К-4, К-6).

Изм.	Кол.уч	Лист	№ док.	Подп.	Дата
Разраб.		Кырлан А.С.			04.11.26
Пров.					
ГИП					
Н. контр.					
Утв.					

ГД-2026-008-АИ

Квартира с кабинетом

Общая площадь 127,29* м² · * размеры со скана, не замерены (реестр — л. 6–8, К-1)

	Стадия	Лист	Листов
Дизайн-проект интерьера	РП	9	131

Задание на контрольный обмер и обследование.
Лист 1 из 3
М б/м

Кырлан Александр Сергеевич

выпуск 04.11.2026 № 4177cbe7a3 · стр. 9 из 166

Задание на контрольный обмер и обследование. Лист 2 из 3

ПРЕДВАРИТЕЛЬНО · не для производства работ · открыто пунктов: 13 (реестр — л. 6–8)

Что замерить, вскрыть и получить до заказа материалов и изделий

Этап 1. До демонтажа (продолжение)

№	Где	Способ	Что сделать	Кто выполняет	Точность	Что пересчитается в альбоме	Чем подтверждается	Закрывает вопросы реестра
О-5	Все помещения квартиры	Обмер	Высота потолка в каждом помещении в нескольких точках: центр, углы, у проёмов.	Архитектор	±5 мм	Вертикальные размеры альбома: развёртки, шкафы, плитка, объёмы работ. Листы: л. 2–5 — Общие данные	акт контрольного обмера	К-2 Результат принимает: Архитектор
О-6	По месту	Обмер	Подтвердить на объекте принятое: подрайон климата не задан — принят не северный (жилые от 2,5 м)	Архитектор	±5 мм	Листы, где используется принятая величина. Листы: л. 2–5 — Общие данные	акт контрольного обмера	К-6 Результат принимает: Архитектор
О-7	пом. 9, стояк Ст К1-1	Обмер	Отметка низа врезки (тройника) в стояк Ст К1-1 от плиты перекрытия и тип стояка.	исполнитель	±5 мм	высота подиума, профиль К1 (схема разводки) Листы: л. 36 — План выводов сантехники л. 37 — Схема разводки водопровода и канализации л. 58 — План полов	фото с рулеткой и привязкой к стене или углу	К-10 Результат принимает: Инженер ВК (вода, канализация)

Этап 2. После демонтажа, до черновых работ

№	Где	Способ	Что сделать	Кто выполняет	Точность	Что пересчитается в альбоме	Чем подтверждается	Закрывает вопросы реестра
О-8	Спальня (пом. 1), Гардеробная-постирочная (пом. 2), Кабинет (пом. 3), Кухня-гостиная (пом. 4), Коридор (пом. 5), Детская (пом. 6), Ванная (пом. 7), Прихожая (пом. 8), Санузел гостевой (пом. 9)	Обмер	Нивелировка плиты перекрытия и существующего пола после демонтажа покрытий: отметки в углах и по сетке, перепады по помещению, уклоны, отметки порогов (чистый пол в мокрых зонах принят -15 мм, 0 мм). Принятая толщина стяжки 33 мм, 50 мм и отметка чистого пола — расчётные, не от замера плиты.	Архитектор	±5 мм по отметке; ровность просвет под 2-метровой рейкой, горизонталь против 0,2 % длины помещения	Толщина стяжки и отметка чистого пола; уклоны к трапам и пороги; выпуски К1 относительно чистого пола (план разводки); объёмы стяжки и смеси в ВОР и спецификации. Листы: л. 54, 58 — План полов л. 37 — Схема разводки водопровода и канализации	акт контрольного обмера	Вопроса в реестре нет: Альбом принимает отметки плиты и толщину пирога пола без нивелировки. Результат принимает: Отделочник
О-9	Спальня (пом. 1), Гардеробная-постирочная (пом. 2), Кабинет (пом. 3), Кухня-гостиная (пом. 4), Коридор (пом. 5), Детская (пом. 6), Ванная (пом. 7), Прихожая (пом. 8), Санузел гостевой (пом. 9)	Обмер	Вертикаль и плоскостность стен: отклонение от вертикали по высоте стены (отвес или лазерный уровень), просвет под правилом 2 м, кривизна углов. Нужно там, где от стены зависит изделие: облицовка плиткой (пом. 7, 9), штукатурка и окраска (пом. 1, 2, 3, 4, 5, 6, 7, 8, 9), встроенная мебель и кухня (пом. 3, 4, 6, 8).	Архитектор	до 1 мм на 2 м (правило и клиновой щуп); вертикаль — мм на высоту стены, отклонения подписываются на плане	Толщина штукатурки и расход смеси в ВОР и спецификации; раскладка плитки (подрезка у стен); зазоры и крепление встроенной мебели и кухни. Листы: л. 54–57 — Раскладка плитки л. 59, 60 — Ведомость отделки помещений	акт контрольного обмера	Вопроса в реестре нет: Альбом принимает стены ровными и вертикальными без замера. Результат принимает: Отделочник

Допущения и предложения на листе

Основа листа: размеры сняты с растрового плана заказчика с частичными размерами: рисунок не в масштабе, помещения выровнены по подписанным размерам мебели и проходов; контрольный обмер не выполнен (К-1); высота потолка 2700 мм принята: на плане заказчика её нет (К-2); толщины стен 300 / 120 мм приняты по плану заказчика, не замерены (К-1); разрешённая мощность 15 кВт принята по типовым ТУ для квартиры, ТУ заказчиком не переданы (К-4); подрайон климата не задан — принят не северный (жилые от 2,5 м) (К-6).
См. лист открытых вопросов (лист 6, записи К-1, К-2, К-4, К-6).

Изм.	Кол.уч	Лист	№ док.	Подп.	Дата
Разраб.		Кырлан А.С.			04.11.26
Пров.					
ГИП					
Н. контр.					
Утв.					

ГД-2026-008-АИ

Квартира с кабинетом

Общая площадь 127,29* м² · * размеры со скана, не замерены (реестр — л. 6–8, К-1)

Дизайн-проект интерьера

Стадия	Лист	Листов
РП	10	131

Задание на контрольный обмер и обследование.
Лист 2 из 3
М б/м

Кырлан Александр Сергеевич

выпуск 04.11.2026 № 4177cbe7a3 · стр. 10 из 166

Задание на контрольный обмер и обследование. Лист 3 из 3

ПРЕДВАРИТЕЛЬНО · не для производства работ · открыто пунктов: 13 (реестр — л. 6–8)

Что замерить, вскрыть и получить до заказа материалов и изделий

Этап 3. После черновых работ, до чистового пола

№	Где	Способ	Что сделать	Кто выполняет	Точность	Что пересчитается в альбоме	Чем подтверждается	Закрывает вопросы реестра
О-10	Кухня-гостиная (пом. 4): Кх12*	Обмер	Положение и габариты по готовым стенам и по месту: Кх12* (тв-стена встроенная 1800×400 h 2500). Принято по проекту, подтвердить на объекте перед заказом и монтажом. Основание допущения: Было: предмет 1800×400 h 500 на отметке 0 — на развёртке стены Б низкий короб у пола. Стало: встроенная ТВ-стена до потолка — каркас на стене и облицовка панелями, с нишами ТВ и биокамина; размеры и отметки ниш, облицовка ниши камина и каркас — предложение исполнителя (ИЗ-5), заказчиком не утверждены. Биокамин — оборудование: модель, мощность, зазоры по паспорту и приток — вопрос К-13; биокамин оставлен решением автора (ИЗ-9); модель не выбрана — зазоры и приток по паспорту..	Архитектор	±5 мм	Габариты и привязки предметов на планах расстановки и развёртках; выводы электрики и ВК, если они привязаны к предмету. Листы: л. 20 — План расстановки мебели	акт контрольного обмера	К-20 Результат принимает: Мебельщик

Документы и данные закупки (не на объекте)

№	У кого, откуда	Способ	Что получить	К какому сроку	Что пересчитается в альбоме	Чем подтверждается	Закрывает вопросы реестра
О-11	Заказчик; организация, выдавшая технические условия	Документ	Технические условия на присоединение: разрешённая мощность.	До утверждения однолинейной схемы щита	Однолинейная схема щита: вводной аппарат и группы. Листы: л. 2–5 — Общие данные	копия документа	К-4 Результат принимает: Инженер-электрик
О-12	вся квартира	Документ	Поэтажный план БТИ и техническое заключение о несущих стенах.	до демонтажа и возведения перегородок	монтажный план, проёмы, развёртки Листы: л. 15 — Обмерный план	копия документа	К-5 Результат принимает: Архитектор
О-13	адрес объекта, СП 131.13330	Документ	Климатический подрайон по СП 131.13330 (по адресу объекта)	до заказа каркаса потолков	план потолков, разрезы, ведомость объёмов Листы: л. 48 — План потолков	копия документа	К-6 Результат принимает: Архитектор

Примечания

1. Подтверждение: акт контрольного обмера (дата, кто присутствовал, прибор, перечень промеров с результатами, подписи присутствующих); к акту — фото вскрытий и узлов и техническое заключение организации, выполнившей обследование.
2. Номера листов — по ведомости рабочих чертежей комплекта (лист «Общие данные»).
3. Пункт исключается из задания при следующем выпуске, когда акт подписан, значение внесено в проект и листы перевыпущены; знак «*» у величины снимается только замером.

Допущения и предложения на листе

Основа листа: размеры сняты с растрового плана заказчика с частичными размерами: рисунок не в масштабе, помещения выровнены по подписанным размерам мебели и проходов; контрольный обмер не выполнен (К-1); высота потолка 2700 мм принята: на плане заказчика её нет (К-2); толщины стен 300 / 120 мм приняты по плану заказчика, не замерены (К-1); разрешённая мощность 15 кВт принята по типовым ТУ для квартиры, ТУ заказчиком не переданы (К-4); подрайон климата не задан — принят не северный (жилые от 2,5 м) (К-6).
Знак «*» — принято, не замерено и не подтверждено (замерить на объекте): ИЗ-5, ИЗ-9, К-20: Кх12 — Было: предмет 1800×400 h 500 на отметке 0 — на развёртке стены Б низкий короб у пола.
См. лист открытых вопросов (лист 6, записи К-1, К-2, К-4, К-6; лист 7, запись К-20; лист 8, записи ИЗ-5, ИЗ-9).

Изм.	Кол.уч	Лист	№ док.	Подп.	Дата
Разраб.		Кырлан А.С.			04.11.26
Пров.					
ГИП					
Н. контр.					
Утв.					

ГД-2026-008-АИ

Квартира с кабинетом

Общая площадь 127,29* м² · * размеры со скана, не замерены (реестр — л. 6–8, К-1)

Дизайн-проект интерьера

Стадия	Лист	Листов
РП	11	131

Задание на контрольный обмер и обследование.
Лист 3 из 3
М б/м

Кырлан Александр Сергеевич

График закупок и работ. Лист 1 из 3

ПРЕДВАРИТЕЛЬНО · не для производства работ · открыто пунктов: 13 (реестр — л. 6–8)

Что заказывать и когда не раньше чего: относительный порядок без дат; срок поставки — из данных или «не задан» с записью реестра

Лист не содержит дат: контрольного обмера, подписанных решений автора и договоров ещё нет, и любая дата была бы выдумана. Вместо календаря — порядок и условия: замер → решение и выбор изделия → заказ → срок поставки → работа, которую позиция блокирует. Срок поставки печатается как срок, только если он задан в данных позиции. Нет — «срок поставки не задан» и ссылка на вопрос реестра о сроках; типовой диапазон практики стоит рядом как ориентир и заказывать по нему нельзя. Номера З-N и Р-N — строки этого листа, К-N — записи реестра открытых вопросов, О-N — позиции задания на контрольный обмер.

Закупки: что заказывается, от чего зависит заказ и какую работу блокирует

№	Позиция и где	1. Замер до заказа	2. Решение, выбор изделия, паспорт	3. Условие заказа	4. Срок поставки	5. Блокирует работу	Закрывает вопросы реестра
З-1	Двери скрытого монтажа с коробом под покраску в существующих проёмах: Д-2, Д-3, Д-4, Д-5, Д-6, Д-7 — 6 шт. пом. 1, 2, 3, 6, 7, 8	О-4: обмер: все помещения (К-1); до заказа мебели и дверей		После 1 и 2 и после получения срока у поставщика (вопроса о сроках нет); дата заказа — когда срок известен, не позднее чем за срок до начала Р-5.	срок поставки не задан (записи реестра нет) Ориентир практики (не срок поставщика): ≈ 30 дн.	Р-5 «штукатурка»: короб ставят до штукатурки (коробку ставят на черновой стадии; полотно навешивают после чистовой отделки стен)	К-1
З-2	Кухонный гарнитур по проекту кухни: модули Кх1, Кх2, Кх3, Кх4, Кх5 пом. 4			После 1 и 2 и после получения срока у поставщика (вопроса о сроках нет); дата заказа — когда срок известен, не позднее чем за срок до начала Р-15.	срок поставки не задан (записи реестра нет) Ориентир практики (не срок поставщика): 4–8 нед. от замера	Р-15 «кухня и мебель»: замер кухни — по готовым стенам после штукатурки или плитки, до чистового пола; производство идёт параллельно со стяжкой и отделкой	
З-3	Встраиваемая техника кухни: Кх1 холодильник, Кх3 посудомоечная машина, Кх5 oven пом. 4			После 1 и 2 и после получения срока у поставщика (вопроса о сроках нет); дата заказа — когда срок известен, не позднее чем за срок до начала Р-15.	срок поставки не задан (записи реестра нет)	Р-15 «кухня и мебель»: паспорта и монтажные схемы — до изготовления модулей кухни: нишу и вентзазоры задаёт модель, а не типовая схема 60 см	
З-4	Стиральная машина: П6 (вертикальная загрузка 400 × 600 мм — условие закупки) пом. 7			После 1 и 2 и после получения срока у поставщика (вопроса о сроках нет); дата заказа — когда срок известен, не позднее чем за срок до начала Р-4.	срок поставки не задан (записи реестра нет)	Р-4 «черновая сантехника»: габарит и подводка — до закрытия люка и разводки	
З-5	Сантехнические приборы и инсталляции: П1**, П2, П3, П4, П5, П10**, П11, П12 пом. 7, 9	О-3: обмер: Кухня-гостиная (пом. 4); у окон		После 1 и 2 и после получения срока у поставщика (вопроса о сроках нет); дата заказа — когда срок известен, не позднее чем за срок до начала Р-4.	срок поставки не задан (записи реестра нет)	Р-4 «черновая сантехника»: инсталляцию ставят до обшивки ГКЛВ и до гидроизоляции стены	
З-6	Керамогранит и плитка: 3 поз. по артикулу и формату, 73,44 м² по раскладке пом. 4, 7, 8, 9	О-8: обмер: Спальня (пом. 1), Гардеробная-постирочная (пом. 2), Кабинет (пом. 3), Кухня-гостиная (пом. 4), Коридор (пом. 5), Детская (пом. 6), Ванная (пом. 7), Прихожая (пом. 8), Санузел гостевой (пом. 9) О-9: обмер: Спальня (пом. 1), Гардеробная-постирочная (пом. 2), Кабинет (пом. 3), Кухня-гостиная (пом. 4), Коридор (пом. 5), Детская (пом. 6), Ванная (пом. 7), Прихожая (пом. 8), Санузел гостевой (пом. 9)		После 1 и 2 и после получения срока у поставщика (вопроса о сроках нет); дата заказа — когда срок известен, не позднее чем за срок до начала Р-9.	срок поставки не задан (записи реестра нет)	Р-9 «плитка»: калибр партии измеряют до раскладки, раскладку пересчитывают до заказа	
З-7	Покрытие пола (доска) и плинтус: пом. 1, 2, 3, 4, 5, 6 пом. 1, 2, 3, 4, 5, 6	О-8: обмер: Спальня (пом. 1), Гардеробная-постирочная (пом. 2), Кабинет (пом. 3), Кухня-гостиная (пом. 4), Коридор (пом. 5), Детская (пом. 6), Ванная (пом. 7), Прихожая (пом. 8), Санузел гостевой (пом. 9)		После 1 и 2 и после получения срока у поставщика (вопроса о сроках нет); дата заказа — когда срок известен, не позднее чем за срок до начала Р-12.	срок поставки не задан (записи реестра нет)	Р-12 «чистовые полы»: артикул и партия — до заказа; доску привозят к чистовым полам	

Допущения и предложения на листе

Основа листа: размеры сняты с растрового плана заказчика с частичными размерами: рисунок не в масштабе, помещения выровнены по подписанным размерам мебели и проходов; контрольный обмер не выполнен (К-1); высота потолка 2700 мм принята: на плане заказчика её нет (К-2); толщины стен 300 / 120 мм приняты по плану заказчика, не замерены (К-1); разрешённая мощность 15 кВт принята по типовым ТУ для квартиры, ТУ заказчиком не переданы (К-4); подрайон климата не задан — принят не северный (жилые от 2,5 м) (К-6). Знак «**» — предложение проектировщика, заказчиком не утверждено (согласовать с заказчиком): К-10: П10 — Душевая зона 900 × 1640 у стены В и подиум 120 мм у трапа (ступень 127 мм) — предложение проектировщика: трап в стяжке 35 мм с облицовкой 14 мм не встаёт (монтажная высота трапа 90 до верха решётки + уклон отвода Ø50 до стояка 78 = 168 мм при врезке на уровне плиты); край подиума у проёма — вариант расстановки за автором; К-11: П1 — Стойка смесителя и выводы ванны в полу — предложение проектировщика; пирог пола — К-11.

Открытые вопросы и конфликты по листу: К-8.

См. лист открытых вопросов (лист 6, записи К-1, К-2, К-4, К-6, К-8, К-10, К-11).

Изм.	Кол.уч	Лист	№ док.	Подп.	Дата
Разраб.		Кырлан А.С.			04.11.26
Пров.					
ГИП					
Н. контр.					
Утв.					

ГД-2026-008-АИ

Квартира с кабинетом

Общая площадь 127,29* м² · * размеры со скана, не замерены (реестр — л. 6–8, К-1)

	Стадия	Лист	Листов
Дизайн-проект интерьера	РП	12	131

График закупок и работ. Лист 1 из 3

М б/м

Кырлан Александр Сергеевич

выпуск 04.11.2026 № 4177cbe7a3 · стр. 12 из 166

График закупок и работ. Лист 2 из 3

Что заказывать и когда не раньше чего: относительный порядок без дат; срок поставки — из данных или «не задан» с записью реестра

Закупки: что заказывается, от чего зависит заказ и какую работу блокирует (продолжение)

№	Позиция и где	1. Замер до заказа	2. Решение, выбор изделия, паспорт	3. Условие заказа	4. Срок поставки	5. Блокирует работу	Закрывает вопросы реестра
З-8	Встроенная мебель по замеру цеха: Кб1, Кх12*, Кх13, Дт1, Пх1** пом. 3, 4, 6, 8	О-10: обмер: Кухня-гостиная (пом. 4): Кх12* (К-20) О-4: обмер: все помещения (К-1); до заказа мебели и дверей		После 1 и 2 и после получения срока у поставщика (вопроса о сроках нет); дата заказа — когда срок известен, не позднее чем за срок до начала Р-15.	срок поставки не задан (записи реестра нет) Ориентир практики (не срок поставщика): 4–8 нед. от замера	Р-15 «кухня и мебель»: цех замеряет по готовым стенам; производство 4–8 недель идёт параллельно с отделкой	К-1, К-20

Работы: порядок и что не даёт начать

№	Работа (стадия технологической последовательности)	После	Что должно быть к началу: условия и закупки	Не начинать, пока открыто в реестре
Р-1	Демонтаж покрытий, отделки стен и потолков, дверных блоков и приборов; конструкции, стены и перегородки не трогать до технического заключения (стадия 1)		до начала: запрошены документы на дом и БТИ; контрольный обмер до демонтажа (что видно) сделан	
Р-2	Контрольный обмер на голых стенах и обследование (задание — лист «Задание на контрольный обмер») (стадия 2)	Р-1	после снятия отделки: видны стояки, каналы, щиток, толщины стен; до заказа всего, что делают по размеру	
Р-3	Черновая электрика: штробы, короба, гофра, подрозетники, щит (стадия 4)	Р-2	до начала: план электрики с высотами утверждён; штробы в стенах — только после технического заключения; мебель расставлена	К-4: Разрешённая мощность квартиры по ТУ неизвестна, принята 15 кВт.
Р-4	Черновая сантехника и вентиляция: разводка, выводы, инсталляции, короба стояков (стадия 5)	Р-2	до начала: положение стояков замерено; модели инсталляций и машины выбраны (габариты рамы, подводка); инсталляцию ставят до обшивки ГКЛВ и до гидроизоляции Закупки к началу: З-4 (стиральная машина), З-5 (сантехника)	
Р-5	Коробки скрытых дверей, затем штукатурка стен и откосов (стадия 6)	Р-2, Р-3, Р-4	до начала: электрика и сантехника смонтированы, штробы заделаны; коробки скрытых дверей установлены до штукатурки (поэтому заказ дверей — раньше работы) Закупки к началу: З-1 (двери скрытого монтажа)	К-1: Размеры квартиры сняты с растрового плана заказчика с частичными размерами (рисунок не в масштабе): помещения выровнены по подписанным размерам мебели и проходов.
Р-6	Стяжка пола и тёплый пол (стадия 7)	Р-5	до начала: штукатурка сделана; трубы под стяжкой приняты; нивелировка плиты выполнена	
Р-7	Гидроизоляция санузлов и тест проливом (стадия 8)	Р-6	до начала: стяжка набрала прочность и сухая по инструкции гидроизоляции; выводы стоят на проектных отметках	
Р-8	ГКЛ: короба инсталляции и стояков, ниши, потолки (стадия 9)	Р-3, Р-4	до начала: черновые сети в зоне коробов приняты; закладные под тяжёлое и карнизы стоят; светильники выбраны (вырезы)	
Р-9	Плитка и керамогранит: стены, затем пол; фартук (стадия 10)	Р-6, Р-7, Р-8	до начала: гидроизоляция принята; плитка выбрана, калибр партии измерен, раскладка пересчитана и подписана Закупки к началу: З-6 (плитка)	
Р-10	Шпаклёвка стен и потолков под окраску (стадия 11)	Р-5, Р-8, Р-9	до начала: плитка готова (грязные работы закончены); штукатурка и ГКЛ сухие	
Р-11	Окраска стен, потолков, откосов (стадия 13)	Р-10	до начала: шпаклёвка отшлифована и огрунтована; выкрасы утверждены, колеровка одной партией	
Р-12	Чистовые полы: инженерная доска (стадия 14)	Р-9, Р-11	до начала: влажность основания в норме, мокрые работы закончены; доска выбрана и привезена Закупки к началу: З-7 (доска и плинтус)	
Р-13	Полотна межкомнатных дверей, плинтусы, пороги (стадия 15)	Р-11, Р-12	до начала: чистовой пол уложен; полотна скрытых дверей — после чистовой отделки стен	

Допущения и предложения на листе

Основа листа: размеры сняты с растрового плана заказчика с частичными размерами: рисунок не в масштабе, помещения выровнены по подписанным размерам мебели и проходов; контрольный обмер не выполнен (К-1); высота потолка 2700 мм принята: на плане заказчика её нет (К-2); толщины стен 300 / 120 мм приняты по плану заказчика, не замерены (К-1); разрешённая мощность 15 кВт принята по типовым ТУ для квартиры, ТУ заказчиком не переданы (К-4); подрайон климата не задан — принят не северный (жилые от 2,5 м) (К-6).

Знак «*» — принято, не замерено и не подтверждено (замерить на объекте): ИЗ-5, ИЗ-9, К-20: Кх12 — Было: предмет 1800×400 h 500 на отметке 0 — на развёртке стены Б низкий короб у пола.

Знак «**» — предложение проектировщика, заказчиком не утверждено (согласовать с заказчиком): ИЗ-1: Пх1 — фасад купе по кадру визуализации прихожей: МДФ 10 мм, эмаль матовая, латунный профиль, зеркальные арочные вставки (поле 100 мм).

См. лист открытых вопросов (лист 6, записи К-1, К-2, К-4, К-6; лист 7, записи ИЗ-1, К-20; лист 8, записи ИЗ-5, ИЗ-9).

Изм.	Кол.уч	Лист	№ док.	Подп.	Дата
Разраб.		Кырлан А.С.			04.11.26
Пров.					
ГИП					
Н. контр.					
Утв.					

ГД-2026-008-АИ

Квартира с кабинетом

Общая площадь 127,29* м² · * размеры со скана, не замерены (реестр — л. 6–8, К-1)

Дизайн-проект интерьера	Стадия	Лист	Листов
	РП	13	131

График закупок и работ. Лист 2 из 3

М б/м

Кырлан Александр Сергеевич

выпуск 04.11.2026 № 4177cbe7a3 · стр. 13 из 166

График закупок и работ. Лист 3 из 3

Что заказывать и когда не раньше чего: относительный порядок без дат; срок поставки — из данных или «не задан» с записью реестра

Работы: порядок и что не даёт начать (продолжение)

№	Работа (стадия технологической последовательности)	После	Что должно быть к началу: условия и закупки	Не начинать, пока открыто в реестре
Р-14	Чистовая электрика и сантехника: механизмы, светильники, смесители, приборы (стадия 16)	Р-11, Р-13	до начала: отделка готова; механизмы, светильники и приборы выбраны и привезены	
Р-15	Кухня, встроенная и корпусная мебель, бытовая техника (стадия 17)	Р-13, Р-14	до начала: чистовая сантехника и электрика подведены к местам мебели; замер кухни снят по готовым стенам (после штукатурки или плитки, до чистового пола) Закупки к началу: З-2 (кухонный гарнитур), З-3 (техника кухни), З-8 (мебель по замеру)	К-1: Размеры квартиры сняты с растрового плана заказчика с частичными размерами (рисунок не в масштабе): помещения выровнены по подписанным размерам мебели и проходов. К-20: ТВ-стена Кх12*: низ ниши ТВ (+900) — в 150 мм над верхом ниши биокамина (+750).
Р-16	Сдача: осмотр по чек-листу, дефектная ведомость, устранение замечаний (стадия 18)	Р-14, Р-15	до начала: всё смонтировано; акты скрытых работ подписаны	

Примечания

1. Порядок работ — стадии технологической последовательности из 16 позиций, присутствующих в этом проекте (по строкам ведомости объёмов); остальные стадии таблицы knowledge/remont-tehnologiya.md в проекте не встречаются. Длительности работ не печатаются: их нет ни в данных, ни в нормах для этого объекта.
2. Типовые сроки — ориентир практики, не срок поставщика: скрытые двери — короб около 10 дн., полотно под покраску до 3 нед., шпон 4–5 нед., в среднем около 30 дн. (knowledge/workers/foreman.md, п. 2.4 (profil-doors)); кухня и корпусная мебель — 4–8 недель от замера (knowledge/remont-tehnologiya.md, разд. 2; knowledge/workers/foreman.md, п. 2.4). Заказ по ориентиру не назначается: срок получают у поставщика (вопрос реестра), после чего заказ планируют «не позднее чем за срок до начала работы».
3. Условия заказа берутся из реестра открытых вопросов и задания на контрольный обмер: позиция заказывается, когда закрыты замер (графа 1) и решение (графа 2). Закрывать их может только факт или решение автора с подписью; снять строку с листа можно только закрыв запись реестра.
4. Заказ по размеру до контрольного обмера не делают: двери, кухня и встроенная мебель зависят от обмера (К-11, К-13); скрытые двери, кроме того, зависят от решения по нише санузла 2 (проём Д-5 в перегородке П-1).
5. Номера листов — по ведомости рабочих чертежей комплекта (лист «Общие данные»).

Допущения и предложения на листе

Основа листа: размеры сняты с растрового плана заказчика с частичными размерами: рисунок не в масштабе, помещения выровнены по подписанным размерам мебели и проходов; контрольный обмер не выполнен (К-1); высота потолка 2700 мм принята: на плане заказчика её нет (К-2); толщины стен 300 / 120 мм приняты по плану заказчика, не замерены (К-1); разрешённая мощность 15 кВт принята по типовым ТУ для квартиры, ТУ заказчиком не переданы (К-4); подрайон климата не задан — принят не северный (жилые от 2,5 м) (К-6).
Знак «*» — принято, не замерено и не подтверждено (замерить на объекте): ИЗ-5, ИЗ-9, К-20: Кх12 — Было: предмет 1800×400 h 500 на отметке 0 — на развёртке стены Б низкий короб у пола.
См. лист открытых вопросов (лист 6, записи К-1, К-2, К-4, К-6; лист 7, запись К-20; лист 8, записи ИЗ-5, ИЗ-9).

Изм.	Кол.уч	Лист	№ док.	Подп.	Дата
Разраб.		Кырлан А.С.			04.11.26
Пров.					
ГИП					
Н. контр.					
Утв.					

ГД-2026-008-АИ

Квартира с кабинетом

Общая площадь 127,29* м² · * размеры со скана, не замерены (реестр — л. 6–8, К-1)

Дизайн-проект интерьера	Стадия	Лист	Листов
	РП	14	131

График закупок и работ. Лист 3 из 3

М б/м

Кырлан Александр Сергеевич

выпуск 04.11.2026 № 4177cbe7a3 · стр. 14 из 166

01

Архитектурные решения




Кырлан Александр Сергеевич

выпуск 04.11.2026 № 417/cbe7a3 · стр. 15 из 166

Обмерный план

Существующее положение · размеры в мм · отметки от чистого пола

ПРЕДВАРИТЕЛЬНО · не для производства работ · открыто пунктов: 13 (реестр — л. 6–8)

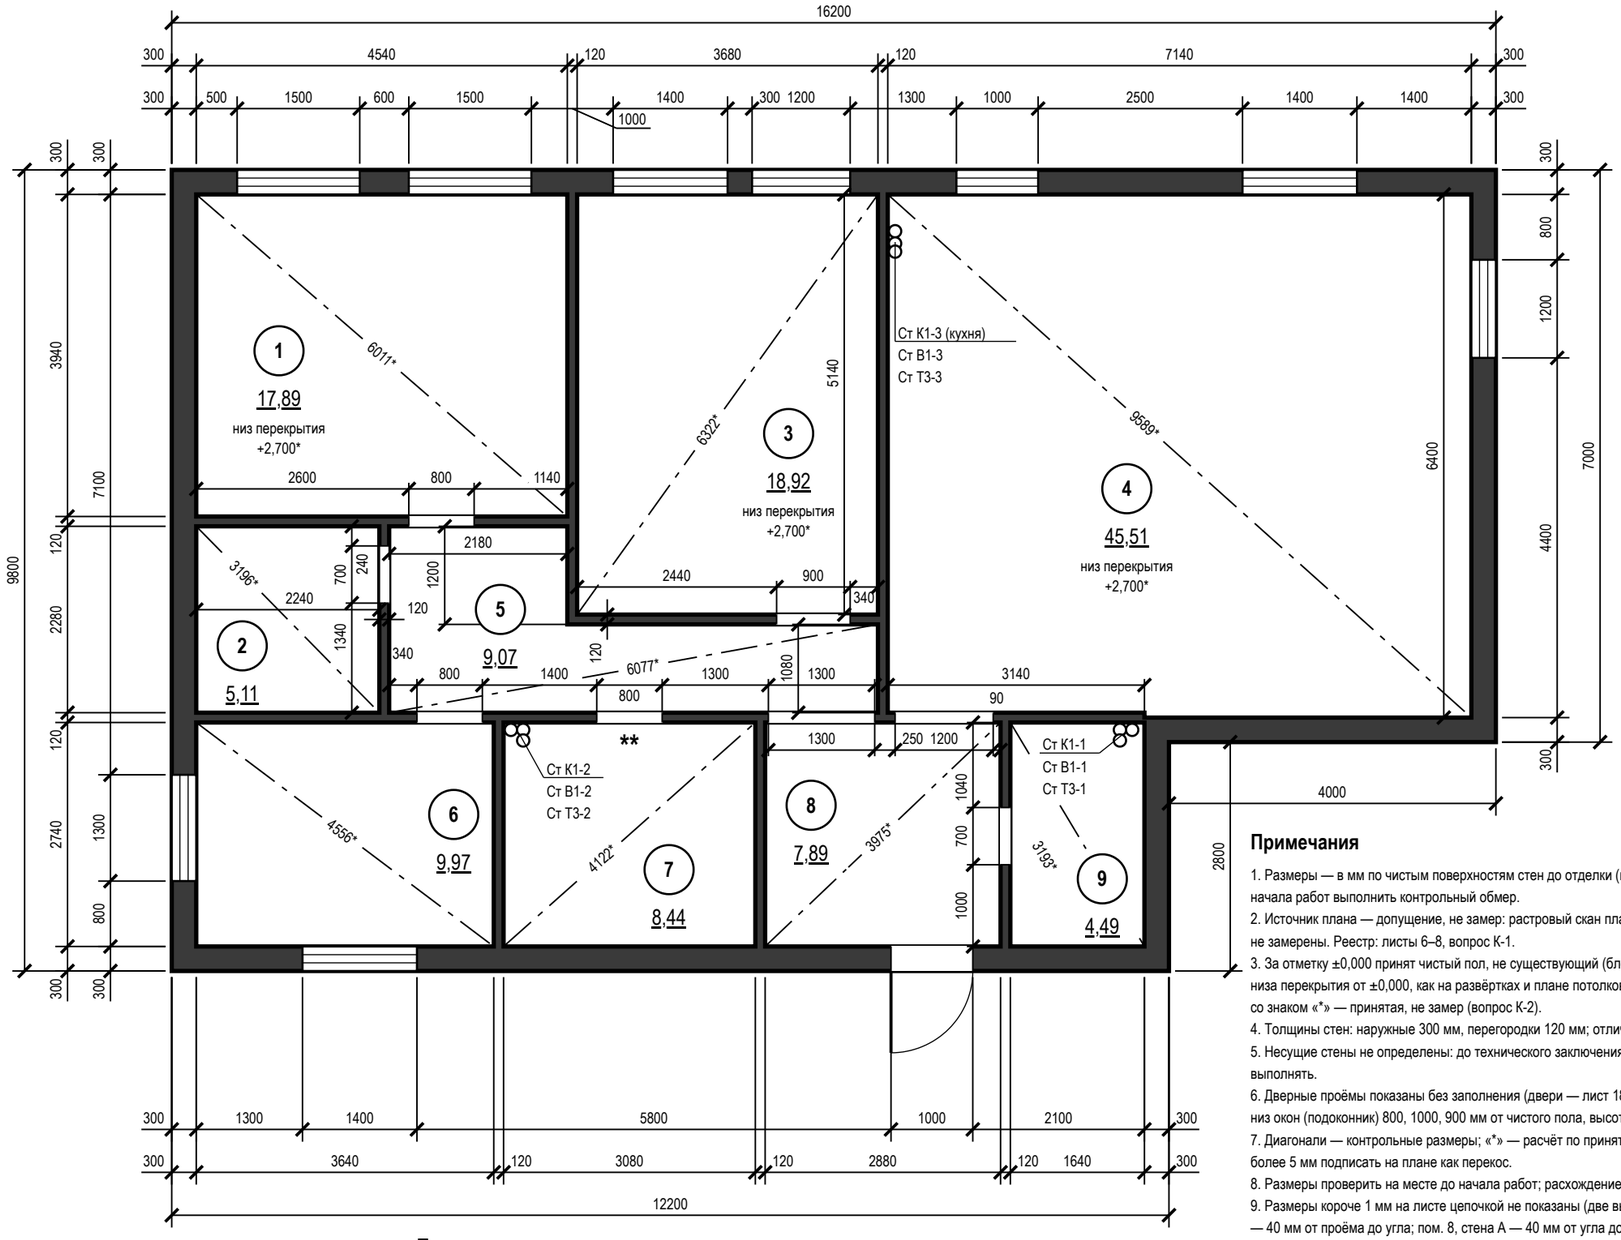

Экспликация помещений

№	Наименование	Площадь, м²
1	Спальня	17,89
2	Гардеробная-постирочная	5,11
3	Кабинет	18,92
4	Кухня-гостиная	45,51
5	Коридор	9,07
6	Детская	9,97
7	Ванная	8,44
8	Прихожая	7,89
9	Санузел гостевой	4,49
	Итого (общая площадь)	**127,29**

Условные обозначения

- существующие стены (сечение)
- окно (рама, остекление)
- проём существующий, без заполнения (откосы)
- стояк: К1 — канализация, В1 — ХВС, Т3 — ГВС
- ** — «**» — предложение проектировщика, заказчиком не утверждено
- диагональ помещения — контроль прямоугольности
- (1) — номер помещения, площадь м²

Примечания

1. Размеры — в мм по чистым поверхностям стен до отделки (по плану заказчика); площади — в м² по тем же размерам. До начала работ выполнить контрольный обмер.
2. Источник плана — допущение, не замер: растровый скан плана заказчика, размеры сняты с размерных цепочек, на объекте не замерены. Реестр: листы 6–8, вопрос К-1.
3. За отметку ±0,000 принят чистый пол, не существующий (блок отметок). «Низ перекрытия» у марки помещения — отметка низа перекрытия от ±0,000, как на развёртках и плане потолков (не высота потолка: потолок — по плану потолков); отметка со знаком «*» — принятая, не замер (вопрос К-2).
4. Толщины стен: наружные 300 мм, перегородки 120 мм; отличающиеся толщины и уступы — размерами на плане.
5. Несущие стены не определены: до технического заключения все стены считать несущими; проёмы и штробы в них не выполнять.
6. Дверные проёмы показаны без заполнения (двери — лист 18); высота дверных проёмов 2100 мм, проёмов без двери 2100 мм; низ окон (подоконник) 800, 1000, 900 мм от чистого пола, высота окон 1600, 1400 мм.
7. Диагонали — контрольные размеры; «*» — расчёт по принятому контуру (К-1), при обмере заменить замеренным; расхождение более 5 мм подписать на плане как перекос.
8. Размеры проверить на месте до начала работ; расхождение контрольных промеров ≤ 2 %.
9. Размеры короче 1 мм на листе цепочкой не показаны (две выносные линии на таком расстоянии сливаются): пом. 5, стена В — 40 мм от проёма до угла; пом. 8, стена А — 40 мм от угла до проёма.

Отметки по высоте

±0,000	чистый пол пом. 1–6, 8; отсчёт высот
−0,015	чистый пол пом. 7, 9, ниже на 15 мм
−0,064*	верх плиты — расчёт, не замер (задание на обмер)
сущ. пол	снимается до плиты; не замерен (задание на обмер)

Принято, не определено или спорно

полностью — листы 6–8

К-7 — Проёмы скрытых дверей Д-2 … Д-7 по плану заказчика высотой 2100 мм, полотно расчётное 2000 мм (ряд UNION FILO-60 Piatto)

Допущения и предложения на листе

Основа листа: размеры сняты с растрового плана заказчика с частичными размерами: рисунок не в масштабе, помещения выровнены по подписанным размерам мебели и проходов; контрольный обмер не выполнен (К-1); высота потолка 2700 мм принята: на плане заказчика её нет (К-2); толщины стен 300 / 120 мм приняты по плану заказчика, не замерены (К-1); разрешённая мощность 15 кВт принята по типовым ТУ для квартиры, ТУ заказчиком не переданы (К-4); подрайон климата не задан — принят не северный (жилые от 2,5 м) (К-6).

Знак «**» — предложение проектировщика, заказчиком не утверждено (согласовать с заказчиком): ИЗ-2, К-5: дверь пом. 7 (стена А) — Проём сдвинут вдоль стены А от угла Б: offset 2300 → 1200 — утверждено автором (ИЗ-2, Кырлан А.С.).

Открытые вопросы и конфликты по листу: К-1, К-2, К-5, К-7.

См. лист открытых вопросов (лист 6, записи К-1, К-2, К-4–К-7; лист 7, запись ИЗ-2).

1000 мм · печать 1:1

Изм.	Кол.уч	Лист	№ док.	Подп.	Дата
Разраб.		Кырлан А.С.			04.11.26
Пров.					
ГИП					
Н. контр.					
Утв.					

ГД-2026-008-АИ

Квартира с кабинетом

Общая площадь 127,29* м² · * размеры со скана, не замерены (реестр — л. 6–8, К-1)

Дизайн-проект интерьера

Стадия	Лист	Листов
РП	15	131

Обмерный план

М 1:75

Кырлан Александр Сергеевич

выпуск 04.11.2026 № 4177cbe7a3 · стр. 16 из 166

План демонтажа и монтажа перегородок

Перепланировка не выполняется · существующие стены сохраняются · размеры в мм

Условные обозначения


- существующие стены — сохраняются;
- несущие не определены — считать несущими
- демонтируемые конструкции — на плане нет
- возводимые перегородки — на плане нет
- проём существующий, без заполнения (откосы)
- (1) номер помещения, площадь м²

Примечания

1. Перепланировка не выполняется: несущие и ненесущие стены, перегородки и плиты перекрытия не демонтируются, новые стены не возводятся; существующие стены и перегородки сохраняются.
2. Дверные блоки — по плану дверей (лист 17); существующие проёмы не расширяются.
3. Демонтаж существующих покрытий пола, стен и потолка, дверных блоков и сантехприборов (если есть) — до основания; объёмы демонтажа — для справки, по факту на объекте.
4. За отметку ±0,000 принят чистый пол, не существующий (блок отметок). Размеры — в мм по чистовой поверхности стен до отделки.
5. Размеры проверить на месте до начала работ: расхождение с обмером — не более 2 % (иначе — к архитектору).
6. Несущие стены не определены: до технического заключения все стены считать несущими — проёмы, ниши и штробы в них не выполнять.

Отметки по высоте

±0,000	чистый пол пом. 1–6, 8; отсчёт высот	**−0,064***	верх плиты — расчёт, не замер (задание на обмер)
−0,015	чистый пол пом. 7, 9, ниже на 15 мм	**сущ. пол**	снимается до плиты; не замерен (задание на обмер)

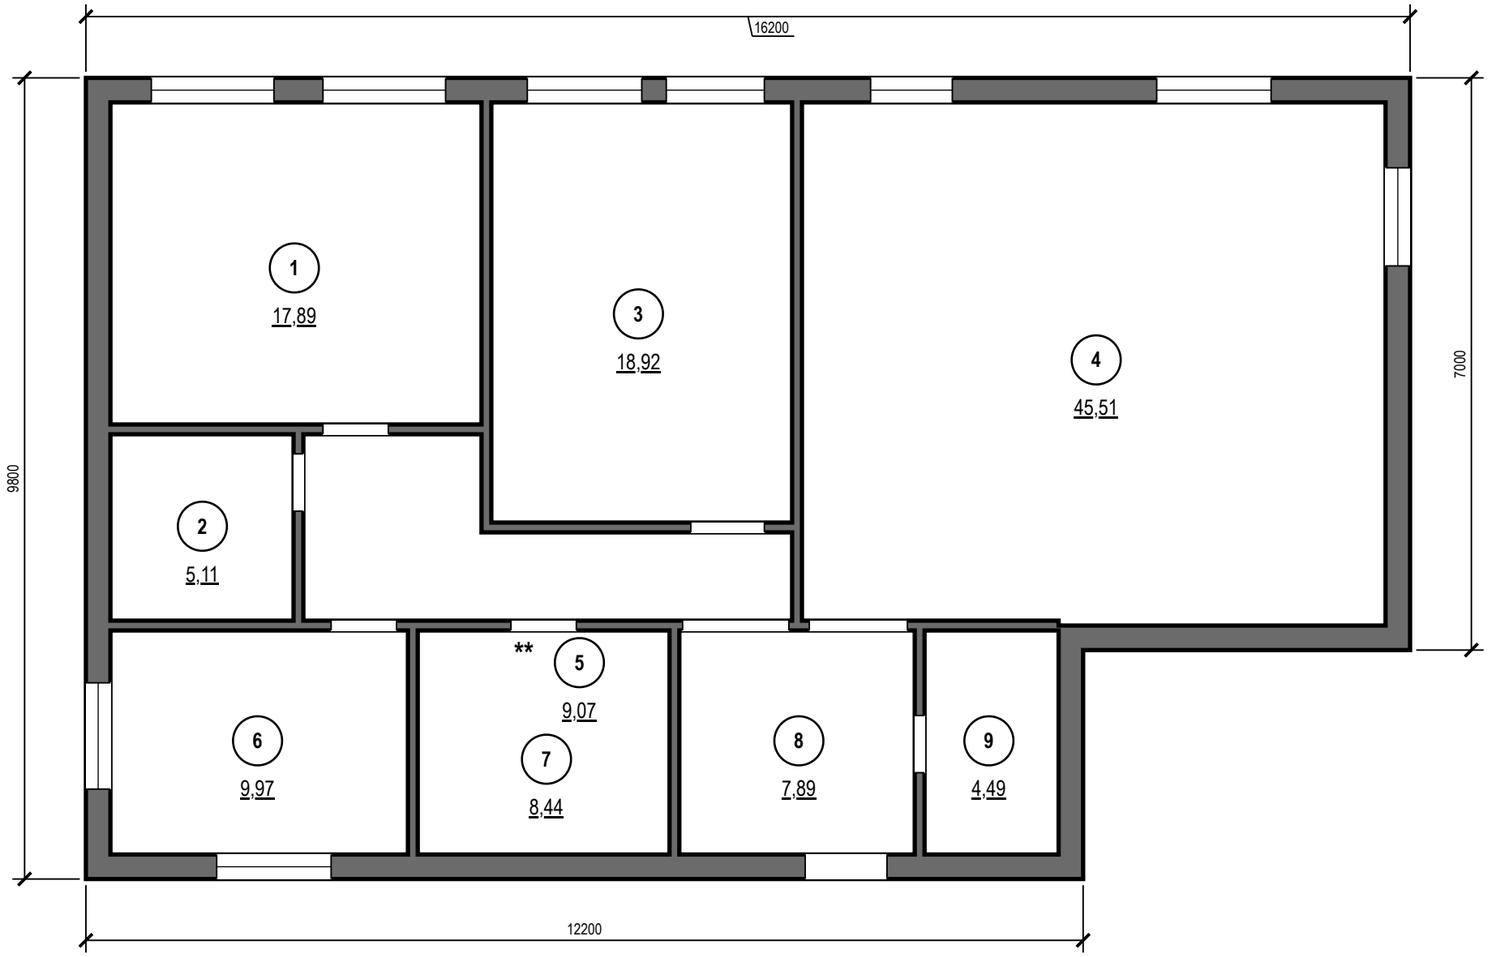

Допущения и предложения на листе

Основа листа: размеры сняты с растрового плана заказчика с частичными размерами: рисунок не в масштабе, помещения выровнены по подписанным размерам мебели и проходов; контрольный обмер не выполнен (К-1); высота потолка 2700 мм принята: на плане заказчика её нет (К-2); толщины стен 300 / 120 мм приняты по плану заказчика, не замерены (К-1); разрешённая мощность 15 кВт принята по типовым ТУ для квартиры, ТУ заказчиком не переданы (К-4); подрайон климата не задан — принят не северный (жилые от 2,5 м) (К-6).
Знак «**» — предложение проектировщика, заказчиком не утверждено (согласовать с заказчиком): ИЗ-2, К-5: дверь пом. 7 (стена А) — Проём сдвинут вдоль стены А от угла Б: offset 2300 → 1200 — утверждено автором (ИЗ-2, Кырлан А.С.).
См. лист открытых вопросов (лист 6, записи К-1, К-2, К-4–К-6; лист 7, запись ИЗ-2).

1000 мм · печать 1:1

Изм.	Кол.уч	Лист	№ док.	Подп.	Дата
Разраб.		Кырлан А.С.			04.11.26
Пров.					
ГИП					
Н. контр.					
Утв.					

ГД-2026-008-АИ

Квартира с кабинетом

Общая площадь 127,29* м² · * размеры со скана, не замерены (реестр — л. 6–8, К-1)

Дизайн-проект интерьера

Стадия	Лист	Листов
РП	16	131

План демонтажа и монтажа перегородок

М 1:75


Кырлан Александр Сергеевич

выпуск 04.11.2026 № 4177cbe7a3 · стр. 17 из 166

План дверей

Проёмы, марки заполнения, привязки · размеры в мм

ПРЕДВАРИТЕЛЬНО · не для производства работ · открыто пунктов: 13 (реестр — л. 6–8)

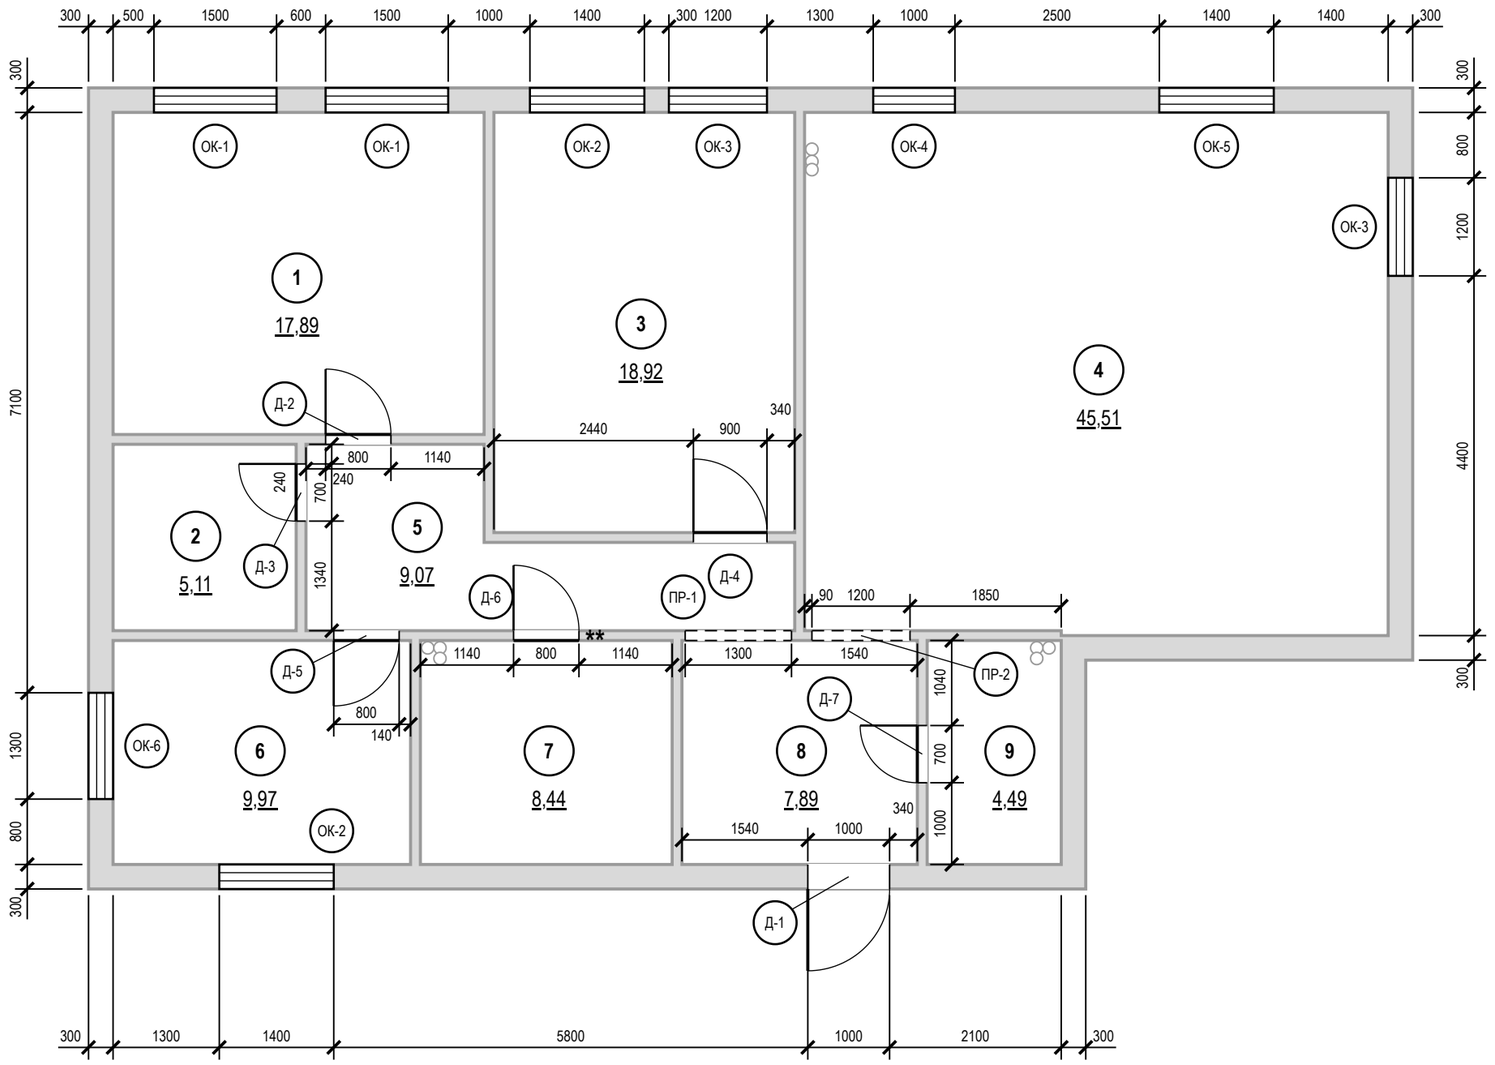

Условные обозначения

- стены (подложка обмера)
- дверь распашная, дуга открывания
- дверь скрытого монтажа
- дверь входная (полотно толще)
- портал (штрих — перемычка)
- оконный блок
- Д — марка типа (Д-N, ПР-N, ОК-N)
- 1 — номер помещения, площадь м²
- ** — «**» — предложение проектировщика, заказчиком не утверждено

Примечания

1. Размеры проёмов и привязки — в миллиметрах от чистых граней стен до отделки; привязка — от угла того помещения, со стороны которого стоит размер. Размер проёма — ширина × высота от чистого пола 0,000. Размеры на плане — проёмов, не полотен: полотно — в ведомости, коробка — по системе. Откос от угла помещения до проёма с коробкой — не менее 50 мм.
2. Марки в кружках — типы заполнения проёмов (ГОСТ 21.501-2018, п. 5.3.2); одна марка — один типоразмер; количество сверено с планом.
3. Д-2…Д-7 — существующие проёмы, до техзаключения не расширять (ИЗ-2, К-5).
4. Д-6, Д-1: дуга наружу — по плану заказчика, не проверено; блок оставить или заменить — не решено (ИЗ-2, К-5).
5. Размеры проёмов и привязки сняты со скана плана заказчика и на объекте не замерены (обмерный план — лист 15).
6. Экспликация помещений — лист 15; в марках помещений — номер и площадь, м².
7. Ведомость заполнения проёмов, открывание полотен, заказ и порядок монтажа блоков — лист 18.
8. Привязка проёма к углу помещения меньше 1 мм на листе, размер на плане не показан: ПР-1 — 40 мм.

Допущения и предложения на листе

Основа листа: размеры сняты с растрового плана заказчика с частичными размерами: рисунок не в масштабе, помещения выровнены по подписанным размерам мебели и проходов; контрольный обмер не выполнен (К-1); высота потолка 2700 мм принята: на плане заказчика её нет (К-2); толщины стен 300 / 120 мм приняты по плану заказчика, не замерены (К-1); разрешённая мощность 15 кВт принята по типовым ТУ для квартиры, ТУ заказчиком не переданы (К-4); подрайон климата не задан — принят не северный (жилые от 2,5 м) (К-6).
Знак «**» — предложение проектировщика, заказчиком не утверждено (согласовать с заказчиком): ИЗ-2, К-5: дверь пом. 7 (стена А) — Проём сдвинут вдоль стены А от угла Б: offset 2300 → 1200 — утверждено автором (ИЗ-2, Кырлан А.С.).
Открытые вопросы и конфликты по листу: К-7, К-8.
См. лист открытых вопросов (лист 6, записи К-1, К-2, К-4–К-8; лист 7, запись ИЗ-2).

1000 мм · печать 1:1

Изм.	Кол.уч	Лист	№ док.	Подп.	Дата
Разраб.		Кырлан А.С.			04.11.26
Пров.					
ГИП					
Н. контр.					
Утв.					

ГД-2026-008-АИ

Квартира с кабинетом

Общая площадь 127,29* м² · * размеры со скана, не замерены (реестр — л. 6–8, К-1)

Дизайн-проект интерьера

Стадия	Лист	Листов
РП	17	131

План дверей

М 1:75

Кырлан Александр Сергеевич


Ведомость заполнения проёмов

Проёмы, полотна, отделка, фурнитура · размеры в мм


Ведомость заполнения проёмов

Марка	Наименование, обозначение	Проём ш×в, мм	Полотно (расч.)	Кол.	Откр.	Отделка полотна	Фурнитура	Прим.
Д-1	Блок дверной входной, ГОСТ 31173-2016	1000×2100	блок задать	1	Л	в комплекте блока	в комплекте блока (замки, глазок)	наружу
Д-2	Дверь скрытого монтажа, UNION FILO-60 Piatto	800×2100	700×2000	1	П	окраска No. 15 с двух сторон	скрытые петли 3D, магнитный замок	
Д-3	Дверь скрытого монтажа, UNION FILO-60 Piatto	700×2100	600×2000	1	Л	V503 — пом. 2, No. 15 — пом. 5	скрытые петли 3D, магнитный замок	
Д-4	Дверь скрытого монтажа, UNION FILO-60 Piatto	900×2100	800×2000	1	П	окраска No. 15 с двух сторон	скрытые петли 3D, магнитный замок	
Д-5	Дверь скрытого монтажа, UNION FILO-60 Piatto	800×2100	700×2000	1	Л	окраска No. 15 с двух сторон	скрытые петли 3D, магнитный замок	
Д-6	Дверь скрытого монтажа, UNION FILO-60 Piatto	800×2100	700×2000	1	П	в тон облицовки с двух сторон	скрытые петли 3D, магнитный замок, фиксатор WC	** пом. 7; порог 15
Д-7	Дверь скрытого монтажа, UNION FILO-60 Piatto	700×2100	600×2000	1	Л	No. 15 — пом. 8, в тон облицовки — пом. 9	скрытые петли 3D, магнитный замок, фиксатор WC	порог 15
ПР-1	Портал без заполнения	1300×2100		1				б/п
ПР-2	Портал без заполнения	1200×2100		1				б/п
ОК-1	Блок оконный, ГОСТ 23166-2021	1500×1600		2				низ 800
ОК-2	Блок оконный, ГОСТ 23166-2021	1400×1600		2				низ 800
ОК-3	Блок оконный, ГОСТ 23166-2021	1200×1600		2				низ 800
ОК-4	Блок оконный, ГОСТ 23166-2021	1000×1400		1				низ 1000
ОК-5	Блок оконный, ГОСТ 23166-2021	1400×1600		1				низ 900
ОК-6	Блок оконный, ГОСТ 23166-2021	1300×1600		1				низ 800

Схемы дверных блоков (1:50) — вид со стороны открывания; вершина треугольника — сторона петель

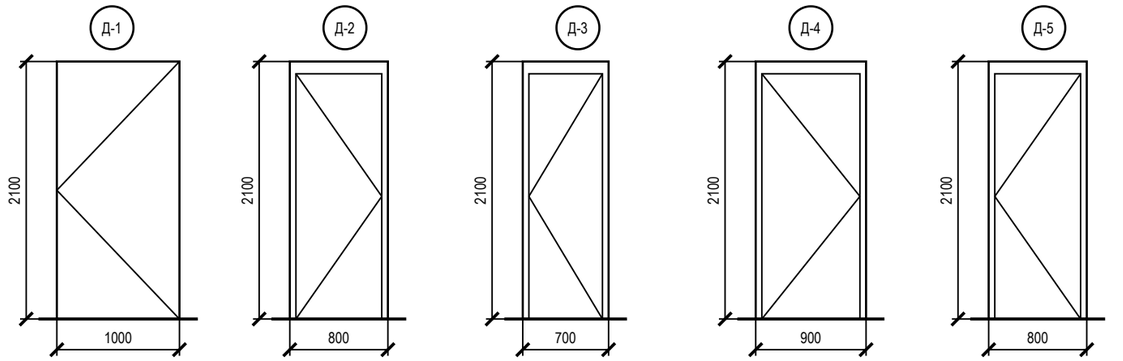

блок — по ГОСТ 31173 откр. Л | полотно 700×2000 (расч.) откр. П | полотно 600×2000 (расч.) откр. Л | полотно 800×2000 (расч.) откр. П | полотно 700×2000 (расч.) откр. Л

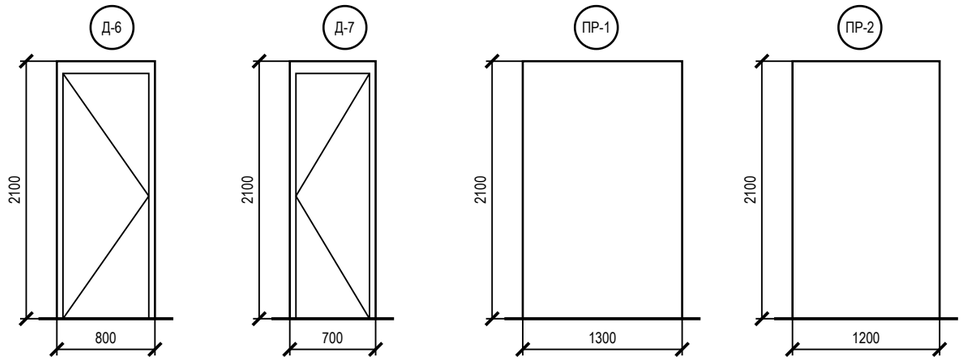

полотно 700×2000 (расч.) откр. П | полотно 600×2000 (расч.) откр. Л | без заполнения | без заполнения

Примечания

1. Марки проёмов — те же, что на плане размещения дверей (лист 17); привязки проёмов — там же.
2. Открывание: Л — петли слева, П — справа, если смотреть со стороны, куда открывается полотно (на себя).
3. Скрытые двери (Д-2…Д-7): проём замерить в чистоте; блок заказать до штукатурки (≈ 30 дн.), короб ставить до штукатурки; полотно навесить после чистовой отделки, красить в цвет стен. Порядок — практика монтажа, изготовитель подтверждает.
4. Полотно «расч.» — по проёму и ряду изделия с запасом по каталогам, заказ — по таблице проёмов модели; Д-2…Д-7: проём 2100, а под полотно 2000 по каталогам нужен 2050–2080, под 2100 — 2150–2180: высоту проёма — по модели; Д-1: входной блок по ГОСТ 31173-2016 — задать при выборе блока.

Допущения и предложения на листе

Основа листа: размеры сняты с растрового плана заказчика с частичными размерами: рисунок не в масштабе, помещения выровнены по подписанным размерам мебели и проходов; контрольный обмер не выполнен (К-1); высота потолка 2700 мм принята: на плане заказчика её нет (К-2); толщины стен 300 / 120 мм приняты по плану заказчика, не замерены (К-1); разрешённая мощность 15 кВт принята по типовым ТУ для квартиры, ТУ заказчиком не переданы (К-4); подрайон климата не задан — принят не северный (жилые от 2,5 м) (К-6).
См. лист открытых вопросов (лист 6, записи К-1, К-2, К-4, К-6).

Изм.	Кол.уч	Лист	№ док.	Подп.	Дата
Разраб.		Кырлан А.С.			04.11.26
Пров.					
ГИП					
Н. контр.					
Утв.					

ГД-2026-008-АИ

Квартира с кабинетом

Общая площадь 127,29* м² · * размеры со скана, не замерены (реестр — л. 6–8, К-1)

Дизайн-проект интерьера	Стадия	Лист	Листов
	РП	18	131

Ведомость заполнения проёмов

М б/м

Кырлан Александр Сергеевич

выпуск 04.11.2026 № 4177cbe7a3 · стр. 19 из 166

02

Планировочное решение

Кырлан Александр Сергеевич

выпуск 04.11.2026 № 417/cbe7a3 · стр. 20 из 166

Концепция интерьера


Модерн (ар-нуво) · схема аналоговая · 60/30/10 · материалы, образы и зонирование

ПРЕДВАРИТЕЛЬНО · не для производства работ · открыто пунктов: 13 (реестр — л. 6–8)


Идея

Стиль — модерн (ар-нуво): природность, плавность, камерность, ремесленность, поэтичность, приглушённая цветность, сумеречный тёплый свет. Модерн 60 % + современный 40 %. Стены — Bone No. 15, потолки — Winter V503, шалфей Calke Green No. 34 и пудровый Peignoir No. 286 вторым планом, акценты — павлиний S 5030-B10G (бархат), горчица India Yellow No. 66, морёный дуб S 8010-Y30R; металл — латунь. Цветовая схема — аналоговая, пропорция 60/30/10: база на стенах и потолках, вторичный цвет — в текстиле и мягкой мебели, акцент — точечно.

Мудборд: материалы и фактуры

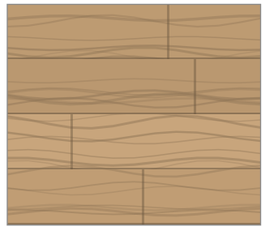

1167-4250
пол

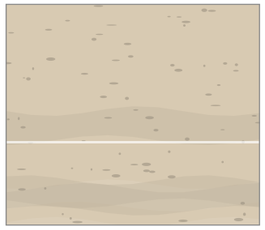

Керамогранит под травертин
фартук




Winter · Tikkurila V503
потолок, стены, плинтус




Bone — мягкий каменно-серый с зеленцой · Farrow & Ball No. 15
стены, плинтус



Calke Green — традиционный шалфей · Farrow & Ball No. 34
акцент (стена А)

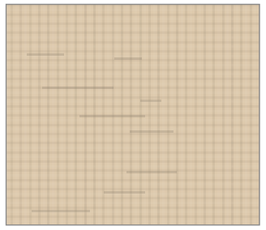


Лён, NCS S 2010-Y30R
портьеры-волна, подушки декоративные на кровать

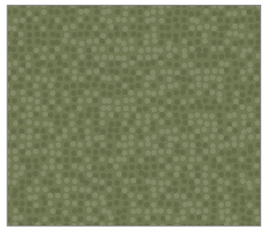

Шерсть, NCS S 5020-G50Y
ковёр под кроватью



Бархат, Farrow & Ball No. 34
подушки на кровать, подушки на диван

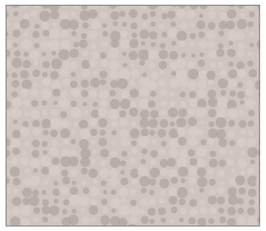

Букле, Farrow & Ball No. 286
подушки декоративные на кровать

Палитра 60/30/10




60 % база — Farrow & Ball No. 15 Bone — мягкий каменно-серый с зеленцой, LRV 53; Tikkurila V503 Winter, LRV 86

30 % вторичный — Farrow & Ball No. 34 Calke Green — традиционный шалфей, LRV 22; Farrow & Ball No. 286 Peignoir серо-розовый, LRV 57

10 % акцент — NCS S 5030-B10G Павлиний сине-зелёный, LRV 12; Farrow & Ball No. 66 India Yellow — глубокая горчица, LRV 36; NCS S 8010-Y30R Тёмно-коричневый, LRV 3

Функциональное зонирование (М 1:200)

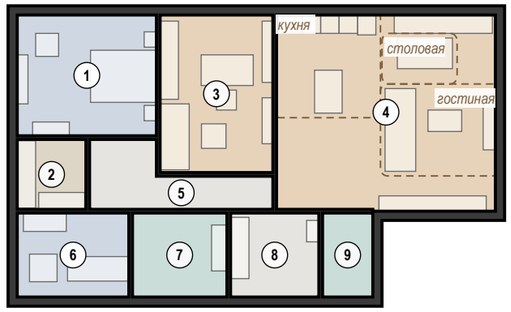

- дневная зона: гостиная, кухня, столовая
- ночная зона: спальни
- мокрая зона: санузлы
- хранение: гардеробная, кладовая
- вход и коммуникации
- функциональная зона в помещении
- (1) номер помещения (лист 20)

Образы помещений

4. Кухня-гостиная — 45,51 м²
стены Farrow & Ball No. 15; акцент No. 34 на стене А
пол — 1167-4250

1. Спальня — 17,89 м²
стены Farrow & Ball No. 15; акцент No. 34 на стене А
пол — 1167-4250

6. Детская — 9,97 м²
стены Farrow & Ball No. 15; акцент No. 34 на стене А
пол — 1167-4250

3. Кабинет — 18,92 м²
стены Farrow & Ball No. 15; акцент No. 34 на стене А
пол — 1167-4250

8. Прихожая — 7,89 м²
стены Farrow & Ball No. 15
пол — A8UZ
декор: зеркало

5. Коридор — 9,07 м²
стены Farrow & Ball No. 15
пол — 1167-4250
свет 3000 K

2. Гардеробная-постирочная — 5,11 м²
стены Tikkurila V503
пол — 1167-4250
свет 3000 K

7. Ванная — 8,44 м²
стены Atlas Concorde A8UZ
пол — керамогранит под травертин, матовый
декор: зеркало над умывальниками

9. Санузел гостевой — 4,49 м²
стены Atlas Concorde A8UZ
пол — керамогранит под травертин, матовый
декор: зеркало над умывальником

Материалы и отделка

1167-4250
пол — пом. 1, 2, 3, 4, 5, 6

Керамогранит под травертин
матовый; 1200×600
фартук — пом. 4

Керамогранит ректифицированный под травертин
матовый; 600×600
пол — пом. 7, 9

A8UZ
стены, пол — пом. 7, 8, 9

Farrow & Ball No. 15 Bone — мягкий каменно-серый с зеленцой, LRV 53
Farrow & Ball Modern Emulsion, матовая
стены, плинтус — пом. 1, 3, 4, 5, 6, 8

Tikkurila V503 Winter, LRV 86
Tikkurila Anti-Reflex 2, глубокоматовая
потолок, стены, плинтус — пом. 1, 2, 3, 4, 5, 6, 7, 8, 9

Farrow & Ball No. 34 Calke Green — традиционный шалфей, LRV 22
акцентная стена
акцент (стена А) — пом. 1, 3, 4, 6

Текстиль и металл

Лён, NCS S 2010-Y30R
портьеры-волна, подушки декоративные на кровать

Вуаль, Tikkurila V503
тюль

Шерсть, NCS S 5020-G50Y
ковёр под кроватью

Бархат, Farrow & Ball No. 34
подушки на кровать, подушки на диван

Шерсть, Farrow & Ball No. 34
плед на кровать

Шерсть, Farrow & Ball No. 66
ковёр под кроватью, ковёр в зоне отдыха

Букле, Farrow & Ball No. 286
подушки декоративные на кровать

Бархат, NCS S 5030-B10G
подушки на кровать

Чёрный матовый металл
зеркало в рост, зеркало

Лён, Farrow & Ball No. 66
римская штора

Чего избегаем

1) Пластиковая волна: гнутые МДФ-фасады и ПВХ-лепнина без пропорций выглядят пародией
2) Смешивать с ар-деко (острая геометрия, хром, чёрный глянец — другой стиль)
3) Холодные белые стены и хром: модерн живёт в приглушённых тёплых тонах и патинированном металле
4) Яркие кислотные зелёные и чистый фиолетовый — нужны землистые, приглушённые
5) Перегрузка: растительный орнамент одновременно на обоях, шторах, ковре и мебели — выбрать одного солиста
6) Витражная плёнка-самоклейка вместо стекла

Допущения и предложения на листе

Основа листа: размеры сняты с растрового плана заказчика с частичными размерами: рисунок не в масштабе, помещения выровнены по подписанным размерам мебели и проходов; контрольный обмер не выполнен (К-1); высота потолка 2700 мм принята: на плане заказчика её нет (К-2); толщины стен 300 / 120 мм приняты по плану заказчика, не замерены (К-1); разрешённая мощность 15 кВт принята по типовым ТУ для квартиры, ТУ заказчиком не переданы (К-4); подрайон климата не задан — принят не северный (жилые от 2,5 м) (К-6).
См. лист открытых вопросов (лист 6, записи К-1, К-2, К-4, К-6).

Примечания

1. Коды цвета — по веерам производителей (колерная карта, лист 61); перед закупкой краски — выкрас на стене объекта под дневным светом и лампами проекта.
2. Материалы — по ведомости отделки (лист 59); мебель, текстиль и декор — по спецификации (лист 21). Образцы доски, керамогранита и тканей утвердить до заказа.
3. Фактуры на листе условные, цвет передан по HEX-значениям производителей: при печати возможны отклонения, решение — только по физическому образцу.

Изм.	Кол.уч	Лист	№ док.	Подп.	Дата
Разраб.		Кырлан А.С.			04.11.26
Пров.					
ГИП					
Н. контр.					
Утв.					

ГД-2026-008-АИ

Квартира с кабинетом

Общая площадь 127,29* м² · * размеры со скана, не замерены (реестр — л. 6–8, К-1)

Дизайн-проект интерьера	Стадия	Лист	Листов
	РП	19	131

Концепция интерьера
М б/м


Кырлан Александр Сергеевич

выпуск 04.11.2026 № 4177cbe7a3 · стр. 21 из 166

План расстановки мебели

Мебель и оборудование · размеры в мм от чистовых стен · марки — по ведомости

ПРЕДВАРИТЕЛЬНО · не для производства работ · открыто пунктов: 13 (реестр — л. 6–8)

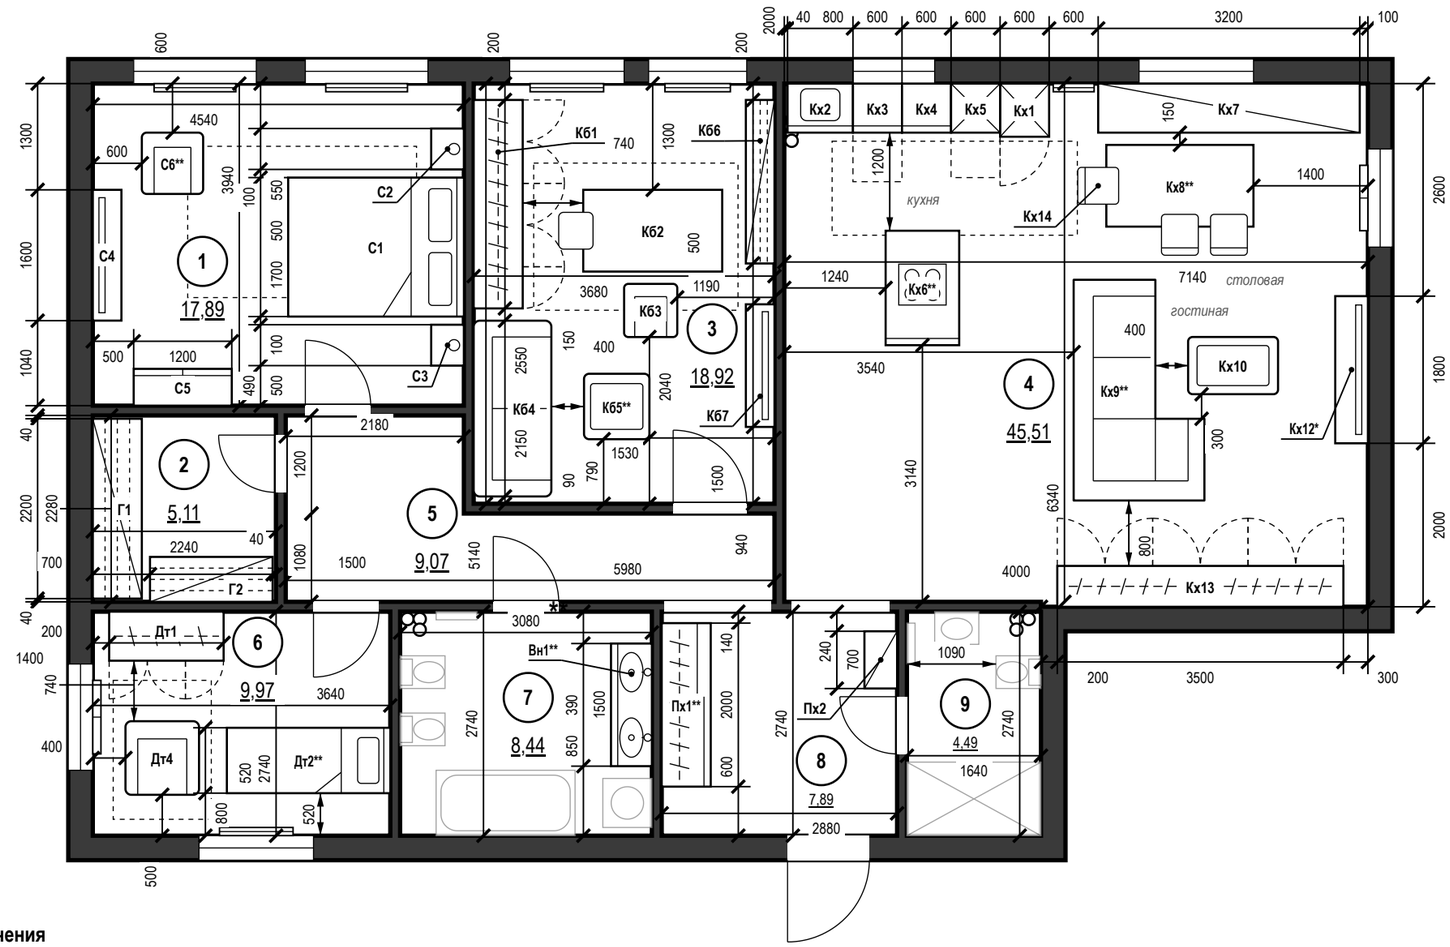

Условные обозначения

- мебель и оборудование — габарит в масштабе
- ковёр
- зона открывания дверец шкафов и техники
- К1 — марка предмета по ведомости мебели
- привязка от чистовой стены, мм
- ширина прохода, зазор, мм
- сантехприборы — подложка (лист ВК)
- радиатор отопления (лист ОВ)
- существующие стены (сечение)
- ** — «**» — предложение проектировщика, заказчиком не утверждено
- стояк: К1 — канализация, В1 — ХВС, Т3 — ГВС
- 1 — номер помещения, площадь м²
- *зона* — функциональная зона помещения

1000 мм · печать 1:1

Примечания

1. Размеры — в мм от чистовых поверхностей стен, размеры помещений — в свету, привязки — от стен, углов помещения и соседних предметов, проходы и зазоры — стрелками; розетки и выводы под мебель — лист 25, выключатели — лист 27, сантехприборы — лист 36.
2. Общие указания к расстановке (чистовой слой, контрольный обмер, зазоры встроенной мебели, замена покупной) — примечания к спецификации, лист 21.
3. Стулья обеденной группы (Кх14 — 3 шт.) показаны в рабочем положении, задвинутыми под столешницу на 150 мм.

Допущения и предложения на листе. Основа листа: размеры сняты с растрового плана заказчика с частичными размерами: рисунок не в масштабе, помещения выровнены по подписанным размерам мебели и проходов; контрольный обмер не выполнен (К-1); высота потолка 2700 мм принята: на плане заказчика её нет (К-2); толщины стен 300 / 120 мм приняты по плану заказчика, не замерены (К-1); разрешённая мощность 15 кВт принята по типовым ТУ для квартиры, ТУ заказчиком не переданы (К-4); подрайон климата не задан — принят не северный (жилые от 2,5 м) (К-6). Знак «*» — принято, не замерено и не подтверждено (замерить на объекте): ИЗ-5, ИЗ-9, К-20: Кх12 — Было: предмет 1800×400 h 500 на отметке 0 — на развёртке стены Б низкий короб у пола. Знак «**» — предложение проектировщика, заказчиком не утверждено (согласовать с заказчиком): Кб5 — Столик отодвинут от дивана Кб4: было 290 мм, меньше практики 300–500 мм — колени упираются в столешницу; ИЗ-1: Кх8 — 6 мест: банкетка Кх7 на 3 места и 3 стула (2 со свободной стороны, 1 у торца) вместо 6 стульев — со стороны банкетки стул не отодвинуть; Кх9 — диван угловой Г 2700 × 1600 (вторая секция 1000 × 1600) по наименованию «угловой модульный»; Дт2 — кровать 800 × 2000 у стены Б, 1480 мм от угла с дверью: вне радиатора РО-9, от открытого полотна Д-5 до кровати 620 мм прохода, вдоль кровати к окну 520 мм; Пх1 — фасад купе по кадру визуализации прихожей: МДФ 10 мм, эмаль матовая, латунный профиль, зеркальные арочные вставки (поле 100 мм); ИЗ-2: Вн1 — Тумба 1500 под раковины П2 и П3 — по описанию модели автора («две на тумбе 1500»): ширина из модели, глубина 500 под раковины 450 и высота столешницы 700 под борт раковин 850, тумба напольная — низ на чистом полу (elevation 0) — предложение проектировщика; выводы ВК под раковинами закрывает тумба; ИЗ-3: С6 — Было х 600, у 3000: кресло 750×750 перекрывало туалетный столик С5 (стена В, 500–1700, глубина 450) на 200 мм по глубине — сесть за столик нельзя, план расходился с кадром визуализации; ИЗ-8: Кх6 — Остров сдвинут от кухонного ряда: торец острова стоял в 900 мм от фронта ПММ Кх3 и модуля Кх4 — меньше 1000 мм (СП 31-107-2004, п. 6.1.12) и меньше 1200 мм, при которых открытые ПММ и ящики не перекрывают проход. См. лист открытых вопросов (лист 6, записи К-1, К-2, К-4–К-6; лист 7, записи ИЗ-1, ИЗ-2, К-20; лист 8, записи ИЗ-3, ИЗ-5, ИЗ-8, ИЗ-9); по листу — К-1.

Экспликация помещений

лист 15 · на плане — номера в марках

Ведомость мебели и оборудования

Марка	Наименование	Ш×Г×В, мм	Пом.	Кол.
С1	Кровать 1700×2150	1700×2150×450	1	1
С2	Тумба прикроватная	500×400×550	1	1
С3	Тумба прикроватная	500×400×550	1	1
С4	ТВ на стене	1600×350×450	1	1
С5	Туалетный столик	1200×450×780	1	1
С6**	Кресло-ракушка	750×750×800	1	1
Г1	Система хранения	2200×600×2400	2	1
Г2	Шкаф	1500×550×2400	2	1
Кб1	Шкаф распашной с арочными фасадами	2550×600×2400	3	1
Кб2	Рабочий стол 1700×1000	1000×1700×750	3	1
Кб3	Кресло рабочее	650×650×900	3	1
Кб4	Диван 2150	2150×950×800	3	1
Кб5**	Столик кофейный круглый	800×800×420	3	1
Кб6	Стеллаж-библиотека с арками	2000×350×2400	3	1
Кб7	ТВ на стене	1500×350×450	3	1
Кх1	Колонна с холодильником	600×650×2100	4	1
Кх2	Модуль под мойку у окна	800×600×900	4	1
Кх3	Посудомоечная машина встроенная	600×600×900	4	1
Кх4	Модуль с ящиками	600×600×900	4	1
Кх5	Колонна	600×600×2100	4	1
Кх6**	Остров 900×1400 с варочной панелью	900×1400×900	4	1
Кх7	Банкетка-диван вдоль окон	3200×600×850	4	1
Кх8**	Стол обеденный овальный 1800×1000	1800×1000×750	4	1
Кх9**	Диван угловой модульный	2700×1600×800	4	1
Кх10	Столик журнальный органической формы	1100×700×380	4	1
Кх12*	ТВ-стена встроенная 1800×400 h	1800×400×2500	4	1
Кх13	Шкаф встроенный	3500×500×2400	4	1
Дт1	Шкаф распашной трёхстворчатый	1400×600×2400	6	1
Дт2**	Кровать 800×2000	800×2000×450	6	1
Дт4	Подвесное кресло-кокон	900×900×1100	6	1
Вн1**	Тумба под две накладные	1500×500×700	7	1
Пх1**	Шкаф-купе с зеркальными арками	2000×600×2500	8	1
Пх2	Пуф и вешалка	700×400×450	8	1
Кх14	Стул обеденный к столу Кх8**	450×500×820	4	3

Ш — вдоль стены (изголовья), Г — от стены (длина кровати)

Материалы, модели, допуск замены — лист 21

Изм.	Кол.уч	Лист	№ док.	Подп.	Дата
Разраб.		Кырлан А.С.			04.11.26
Пров.					
ГИП					
Н. контр.					
Утв.					

ГД-2026-008-АИ

Квартира с кабинетом

Общая площадь 127,29* м² · * размеры со скана, не замерены (реестр — л. 6–8, К-1)

Дизайн-проект интерьера

Стадия	Лист	Листов
РП	20	131

План расстановки мебели

М 1:75

Кырлан Александр Сергеевич

выпуск 04.11.2026 № 4177cbe7a3 · стр. 22 из 166

Спецификация мебели и оборудования

ПРЕДВАРИТЕЛЬНО · не для производства работ · открыто пунктов: 13 (реестр — л. 6–8)

Форма 1 ГОСТ 21.110-2013 · позиции мебели — по плану расстановки

Поз.	Наименование и техническая характеристика	Тип, марка, обозначение документа, опросного листа	Код продукции	Поставщик	Ед. измерения	Кол.	Масса 1 ед., кг	Примечание
	Мебель встроенная и корпусная (изготовление по чертежам мебельщика)							
Г1	Система хранения: штанги, полки, ящики; каркас и полки — ЛДСП 16 мм, декор «дуб натуральный»; без фасадов; Ш×Г×В 2200×600×2400 мм			изготовление на заказ	шт.	1		пом. 2; крепление к стене
Г2	Шкаф с выдвижной гладильной доской и полками; каркас и полки — ЛДСП 16 мм, декор «дуб натуральный»; без фасадов; Ш×Г×В 1500×550×2400 мм			изготовление на заказ	шт.	1		пом. 2; крепление к стене
Кб1	Шкаф распашной с арочными фасадами; корпус ЛДСП 16 мм; фасады — МДФ 18 мм, эмаль матовая; арочная фрезеровка филёнки (полукруглый верх, поле 100 мм); Ш×Г×В 2550×600×2400 мм			изготовление на заказ	шт.	1		пом. 3
Кх1	Колонна с холодильником; корпус ЛДСП 16 мм; фасады — МДФ 18 мм, эмаль матовая; цвет фасадов — в цвет стен (Farrow & Ball No. 15); Ш×Г×В 600×650×2100 мм			изготовление на заказ	шт.	1		пом. 4
Кх2	Модуль под мойку у окна; корпус ЛДСП 16 мм; фасады — МДФ 18 мм, эмаль матовая; цвет фасадов — в цвет стен (Farrow & Ball No. 15); Ш×Г×В 800×600×900 мм			изготовление на заказ	шт.	1		пом. 4
Кх3	Модуль под встраиваемую ПММ 60; без корпуса (ниша между соседними модулями); фасад на дверь машины — МДФ 18 мм, эмаль матовая; цоколь; цвет фасадов — в цвет стен (Farrow & Ball No. 15); Ш×Г×В 600×600×900 мм			изготовление на заказ	шт.	1		пом. 4
Кх4	Модуль с ящиками; корпус ЛДСП 16 мм; фасады — МДФ 18 мм, эмаль матовая; цвет фасадов — в цвет стен (Farrow & Ball No. 15); Ш×Г×В 600×600×900 мм			изготовление на заказ	шт.	1		пом. 4
Кх5	Колонна: духовой шкаф и СВЧ; корпус ЛДСП 16 мм; фасады — МДФ 18 мм, эмаль матовая; цвет фасадов — в цвет стен (Farrow & Ball No. 15); Ш×Г×В 600×600×2100 мм			изготовление на заказ	шт.	1		пом. 4
Кх6**	Остров 900×1400 с варочной панелью, столешница — травертин; корпус ЛДСП 16 мм; фасады — МДФ 18 мм, эмаль матовая; цвет фасадов — в цвет стен (Farrow & Ball No. 15); Ш×Г×В 900×1400×900 мм			изготовление на заказ	шт.	1		пом. 4
Кх7	Банкетка-диван вдоль окон, бархат — экран радиатора, изготовление на заказ; Ш×Г×В 3200×600×850 мм			изготовление на заказ	шт.	1		пом. 4
Кх12*	ТВ-стена встроенная 1800×400 h 2500: каркас на стене Б, панели МДФ с волнистым рельефом (эмаль), ниша ТВ 1500×900 на отметке +900 (низ), ниша биокамина 900×400 на отметке +350 (низ), облицовка ниши камина — негорючая (сталь / камень), вентиляционные зазоры 50 мм над топкой; корпус оцинкованный профиль ПП 60×27 / ПН 28×27 (НГ), на стене Б 27 мм; фасады — панели МДФ 19 мм с волнистым рельефом, эмаль матовая; Ш×Г×В 1800×400×2500 мм			изготовление на заказ	шт.	1		пом. 4
Кх13	Шкаф встроенный, фасады с округлыми торцами; корпус ЛДСП 16 мм; фасады — МДФ 18 мм, эмаль матовая; цвет фасадов — в цвет стен (Farrow & Ball No. 15); Ш×Г×В 3500×500×2400 мм			изготовление на заказ	шт.	1		пом. 4
Дт1	Шкаф распашной трёхстворчатый с антресолью; корпус ЛДСП 16 мм; фасады — МДФ 18 мм, эмаль матовая; цвет фасадов в цвет стен (Farrow & Ball No. 15); Ш×Г×В 1400×600×2400 мм			изготовление на заказ	шт.	1		пом. 6; крепление к стене
Вн1**	Тумба под две накладные раковины П2, П3, 1500 мм, напольная; корпус ЛДСП 16 мм; фасады — МДФ 18 мм, эмаль матовая; цвет фасадов — в цвет стен (Atlas Concorde A8UZ); Ш×Г×В 1500×500×700 мм			изготовление на заказ	шт.	1		пом. 7; крепление к стене
Пх1**	Шкаф-купе с зеркальными арками; корпус ЛДСП 16 мм; фасады — МДФ 10 мм, эмаль матовая в профиле: алюминий, латунь матовая; вставка — зеркало серебро 4 мм, плёнка безопасности, арочная (полукруглый верх, поле 100 мм); Ш×Г×В 2000×600×2500 мм			изготовление на заказ	шт.	1		пом. 8
	Мебель покупная							
С1	Кровать 1700×2150 с высоким округлым изголовьем, бархат; мягкое изголовье, обивка — ткань, цвет Farrow & Ball No. 34; Ш×Г×В 1700×2150×450 мм			аналог по характеристикам	шт.	1		пом. 1; замена ≤ габарита

Примечания

1. Позиции мебели совпадают с марками на плане расстановки (лист 20); размеры Ш×Г×В — Ш вдоль стены, Г от стены.
2. Размеры и привязки плана расстановки — в мм от чистовых поверхностей стен: слой штукатурки 20 мм по блоку и 5 мм шпаклёвки по ГКЛ учтён; привязки — от стен и углов помещения, а не от другой мебели.
3. План расстановки не является документацией для изготовления мебели. Встроенная и корпусная мебель изготавливается по чертежам мебельщика после контрольного обмера (после штукатурки); «стена в стену» — с зазором 10 мм с каждой стороны или с компенсаторами; графы «Тип, марка» и «Код продукции» для неё не заполняются (ГОСТ 21.110-2013).
4. Покупные изделия — аналог по характеристикам: заменять только на изделия не больше указанного габарита и того же материала и цвета.
5. Материал и цвет, не указанные в данных изделия, приняты по концепции (лист 19): тон дерева — по полу, обивка — по вторичному цвету палитры; образцы согласовать до заказа.
6. Масса 1 ед. для изделий до 25 кг не указывается. Техника — по монтажным схемам изготовителя; выводы — по листам ЭОМ и ВК.

Допущения и предложения на листе. Основа листа: размеры сняты с растрового плана заказчика с частичными размерами: рисунок не в масштабе, помещения выровнены по подписанным размерам мебели и проходов; контрольный обмер не выполнен (К-1); высота потолка 2700 мм принята: на плане заказчика её нет (К-2); толщины стен 300 / 120 мм приняты по плану заказчика, не замерены (К-1); разрешённая мощность 15 кВт принята по типовым ТУ для квартиры, ТУ заказчиком не переданы (К-4); подрайон климата не задан — принят не северный (жилые от 2,5 м) (К-6). Знак «*» — принято, не замерено и не подтверждено (замерить на объекте): ИЗ-5, ИЗ-9, К-20: Кх12 — Было: предмет 1800×400 h 500 на отметке 0 — на развёртке стены Б низкий короб у пола. Знак «**» — предложение проектировщика, заказчиком не утверждено (согласовать с заказчиком): ИЗ-1: Пх1 — фасад купе по кадру визуализации прихожей: МДФ 10 мм, эмаль матовая, латунный профиль, зеркальные арочные вставки (поле 100 мм); ИЗ-2: Вн1 — Тумба 1500 под раковины П2 и П3 — по описанию модели автора («две на тумбе 1500»): ширина из модели, глубина 500 под раковины 450 и высота столешницы 700 под борт раковин 850, тумба напольная — низ на чистом полу (elevation 0) — предложение проектировщика; выводы ВК под раковинами закрывает тумба; ИЗ-8: Кх6 — Остров сдвинут от кухонного ряда: торец острова стоял в 900 мм от фронта ПММ Кх3 и модуля Кх4 — меньше 1000 мм (СП 31-107-2004, п. 6.1.12) и меньше 1200 мм, при которых открытые ПММ и ящики не перекрывают проход. См. лист открытых вопросов (лист 6, записи К-1, К-2, К-4, К-6; лист 7, записи ИЗ-1, ИЗ-2, К-20; лист 8, записи ИЗ-5, ИЗ-8, ИЗ-9).

Изм.	Кол.уч	Лист	№ док.	Подп.	Дата
Разраб.		Кырлан А.С.			04.11.26
Пров.					
ГИП					
Н. контр.					
Утв.					

ГД-2026-008-АИ

Квартира с кабинетом

Общая площадь 127,29* м² · * размеры со скана, не замерены (реестр — л. 6–8, К-1)

Дизайн-проект интерьера	Стадия	Лист	Листов
	РП	21	131
Спецификация мебели и оборудования М б/м	**Кырлан Александр Сергеевич**		

выпуск 04.11.2026 № 4177cbe7a3 · стр. 23 из 166

Спецификация мебели и оборудования (продолжение)

ПРЕДВАРИТЕЛЬНО · не для производства работ · открыто пунктов: 13 (реестр — л. 6–8)

Форма 1 ГОСТ 21.110-2013 · позиции мебели — по плану расстановки

Поз.	Наименование и техническая характеристика	Тип, марка, обозначение документа, опросного листа	Код продукции	Поставщик	Ед. измерения	Кол.	Масса 1 ед., кг	Примечание
С2, С3	Тумба прикроватная, морёный дуб, латунные ручки; шпон, дуб натуральный, матовое масло; Ш×Г×В 500×400×550 мм			аналог по характеристикам	шт.	2		пом. 1; замена ≤ габарита
С4	ТВ на стене, тумба подвесная с волнистым фасадом; шпон, дуб натуральный, матовое масло; Ш×Г×В 1600×350×450 мм			аналог по характеристикам	шт.	1		пом. 1; замена ≤ габарита
С5	Туалетный столик с овальным зеркалом в латунной раме; шпон, дуб натуральный, матовое масло; Ш×Г×В 1200×450×780 мм			аналог по характеристикам	шт.	1		пом. 1; замена ≤ габарита
С6**	Кресло-ракушка, бархат павлиньего цвета; обивка — ткань, цвет Farrow & Ball No. 34; Ш×Г×В 750×750×800 мм			аналог по характеристикам	шт.	1		пом. 1; замена ≤ габарита
Кб2	Рабочий стол 1700×1000, морёный дуб, округлые углы; шпон, дуб натуральный, матовое масло; Ш×Г×В 1000×1700×750 мм			аналог по характеристикам	шт.	1		пом. 3; замена ≤ габарита
Кб3	Кресло рабочее, кожа карамельного цвета; обивка — ткань, цвет Farrow & Ball No. 34; Ш×Г×В 650×650×900 мм			аналог по характеристикам	шт.	1		пом. 3; замена ≤ габарита
Кб4	Диван 2150 с мягкими округлыми подлокотниками; обивка — ткань, цвет Farrow & Ball No. 34; Ш×Г×В 2150×950×800 мм			аналог по характеристикам	шт.	1		пом. 3; замена ≤ габарита
Кб5**	Столик кофейный круглый, травертин; шпон, дуб натуральный, матовое масло; Ш×Г×В 800×800×420 мм			аналог по характеристикам	шт.	1		пом. 3; замена ≤ габарита
Кб6	Стеллаж-библиотека с арками; шпон, дуб натуральный, матовое масло; Ш×Г×В 2000×350×2400 мм			аналог по характеристикам	шт.	1		пом. 3; замена ≤ габарита
Кб7	ТВ на стене, тумба подвесная; шпон, дуб натуральный, матовое масло; Ш×Г×В 1500×350×450 мм			аналог по характеристикам	шт.	1		пом. 3; замена ≤ габарита
Кх8**	Стол обеденный овальный 1800×1000, морёный дуб; шпон, дуб натуральный, матовое масло; Ш×Г×В 1800×1000×750 мм			аналог по характеристикам	шт.	1		пом. 4; замена ≤ габарита
Кх9**	Диван угловой модульный с округлыми формами, бархат павлиньего цвета; Г-образный: основная секция 2700, вторая 1000 × 1600 мм; обивка — ткань, цвет Farrow & Ball No. 34; Ш×Г×В 2700×1600×800 мм			аналог по характеристикам	шт.	1		пом. 4; замена ≤ габарита
Кх10	Столик журнальный органической формы, травертин; шпон, дуб натуральный, матовое масло; Ш×Г×В 1100×700×380 мм			аналог по характеристикам	шт.	1		пом. 4; замена ≤ габарита
Кх14	Стул обеденный к столу Кх8**; обивка — ткань, цвет Farrow & Ball No. 34; каркас — дуб натуральный; Ш×Г×В 450×500×820 мм			аналог по характеристикам	шт.	3		пом. 4; замена ≤ габарита
Дт2**	Кровать 800×2000 с мягким изголовьем-облаком; мягкое изголовье, обивка — ткань, цвет Farrow & Ball No. 34; Ш×Г×В 800×2000×450 мм			аналог по характеристикам	шт.	1		пом. 6; замена ≤ габарита
Дт4	Подвесное кресло-кокон; обивка — ткань, цвет Farrow & Ball No. 34; Ш×Г×В 900×900×1100 мм			аналог по характеристикам	шт.	1		пом. 6; замена ≤ габарита
Пх2	Пуф и вешалка; Ш×Г×В 700×400×450 мм			аналог по характеристикам	шт.	1		пом. 8; замена ≤ габарита
	Техника встраиваемая и бытовая (покупные изделия), светильники под розетки							
	Холодильник встраиваемый, в модуле Кх1	аналог по характеристикам: полновстраиваемый под фасад, ниша 1780 × 560 × 550 мм, вентиляция решётка в цоколе, выход сверху		по выбору заказчика до изготовления мебели	шт.	1		пом. 4; по схеме изготовителя
	Посудомоечная машина встраиваемая, в модуле Кх3; ниша 600 мм	аналог по характеристикам: полновстраиваемая 60 см под фасад, ниша 600 × 862 мм, навеска фасада в комплекте		по выбору заказчика до изготовления мебели	шт.	1		пом. 4; по схеме изготовителя
	Духовой шкаф встраиваемый, в модуле Кх5	аналог по характеристикам: 60 см, лицевая панель 595 мм, ниша 568 × 600, глубина ≥ 550 мм, вентиляция за прибором		по выбору заказчика до изготовления мебели	шт.	1		пом. 4; по схеме изготовителя
	СВЧ-печь встраиваемая, в модуле Кх5	аналог по характеристикам: встраиваемая 38 см, лицевая панель 388 мм, ниша 568 × 380, глубина ≥ 550 мм		по выбору заказчика до изготовления мебели	шт.	1		пом. 4; по схеме изготовителя

Допущения и предложения на листе

Основа листа: размеры сняты с растрового плана заказчика с частичными размерами: рисунок не в масштабе, помещения выровнены по подписанным размерам мебели и проходов; контрольный обмер не выполнен (К-1); высота потолка 2700 мм принята: на плане заказчика её нет (К-2); толщины стен 300 / 120 мм приняты по плану заказчика, не замерены (К-1); разрешённая мощность 15 кВт принята по типовым ТУ для квартиры, ТУ заказчиком не переданы (К-4); подрайон климата не задан — принят не северный (жилые от 2,5 м) (К-6).

Знак «**» — предложение проектировщика, заказчиком не утверждено (согласовать с заказчиком): Кб5 — Столик отодвинут от дивана Кб4: было 290 мм, меньше практики 300–500 мм — колени упираются в столешницу; ИЗ-1: Кх8 — 6 мест: банкетка Кх7 на 3 места и 3 стула (2 со свободной стороны, 1 у торца) вместо 6 стульев — со стороны банкетки стул не отодвинуть; Кх9 — диван угловой Г 2700 × 1600 (вторая секция 1000 × 1600) по наименованию «угловой модульный»; Дт2 — кровать 800 × 2000 у стены Б, 1480 мм от угла с дверью: вне радиатора РО-9, от открытого полотна Д-5 до кровати 620 мм прохода, вдоль кровати к окну 520 мм; ИЗ-3: С6 — Было х 600, у 3000: кресло 750×750 перекрывало туалетный столик С5 (стена В, 500–1700, глубина 450) на 200 мм по глубине — сесть за столик нельзя, план расходился с кадром визуализации.

См. лист открытых вопросов (лист 6, записи К-1, К-2, К-4, К-6; лист 7, запись ИЗ-1; лист 8, запись ИЗ-3).

Изм.	Кол.уч	Лист	№ док.	Подп.	Дата
Разраб.		Кырлан А.С.			04.11.26
Пров.					
ГИП					
Н. контр.					
Утв.					

ГД-2026-008-АИ

Квартира с кабинетом

Общая площадь 127,29* м² · * размеры со скана, не замерены (реестр — л. 6–8, К-1)

	Стадия	Лист	Листов
Дизайн-проект интерьера	РП	22	131
Спецификация мебели и оборудования (продолжение) М б/м	**Кырлан Александр Сергеевич**		

Спецификация мебели и оборудования (продолжение)

Форма 1 ГОСТ 21.110-2013 · позиции мебели — по плану расстановки

Поз.	Наименование и техническая характеристика	Тип, марка, обозначение документа, опросного листа	Код продукции	Поставщик	Ед. измерения	Кол.	Масса 1 ед., кг	Примечание
	Вытяжка, над островом Кх6**, потолочная, 900 мм, рециркуляция (угольный фильтр), низ +1,550	аналог по характеристикам: производительность — по расчёту ОВ, шум ≤ 55 дБ(А)		по выбору заказчика до изготовления мебели	шт.	1		пом. 4; по схеме изготовителя
	Варочная панель встраиваемая, индукционная, в модуле Кх6**	аналог по характеристикам: индукционная 60 см, вырез 560 × 490 мм по шаблону модели		по выбору заказчика до изготовления мебели	шт.	1		пом. 4; по схеме изготовителя
	Стиральная машина, место по листу ВК (П6); Ш×Г 600×600 мм	аналог по характеристикам: тип загрузки — по листу ВК, в плане 600 × 600 мм (ширина × глубина), по листу ВК		по выбору заказчика до изготовления мебели	шт.	1		пом. 7; по схеме изготовителя
	Торшер, у поз. С4; абажур — ткань или опаловое стекло; лампа 2700 К			аналог по характеристикам	шт.	1		пом. 1; розетка Р5 (ЭОМ)
	Текстиль							
Т1**	Портьеры-волна; лён 100 %; цвет NCS S 2010-Y30R; карниз 2300 мм, высота 2590 мм, сборка 2			аналог по характеристикам	шт.	2		пом. 1
Т2**	Тюль; полиэстер 100 %; цвет Tikkurila V503; карниз 2300 мм, высота 2590 мм, сборка 2,5			аналог по характеристикам	шт.	1		пом. 1
Т27**	Портьеры-волна; лён 100 %; цвет NCS S 2010-Y30R; карниз 2300 мм, высота 2590 мм, сборка 2			аналог по характеристикам	шт.	2		пом. 1
Т28**	Тюль; полиэстер 100 %; цвет Tikkurila V503; карниз 2300 мм, высота 2590 мм, сборка 2,5			аналог по характеристикам	шт.	1		пом. 1
Т3	Ковёр под кроватью; шерсть 80 %, хлопок 20 %; цвет NCS S 5020-G50Y; 2800×1850 мм			аналог по характеристикам	шт.	1		пом. 1; с подложкой
Т4	Подушки декоративные на кровать; лён 100 %; цвет NCS S 2010-Y30R			аналог по характеристикам	шт.	3		пом. 1
Т5	Подушки на кровать, акцент; хлопковый бархат 100 %; цвет Farrow & Ball No. 34			аналог по характеристикам	шт.	2		пом. 1
Т6	Плед на кровать; шерсть мериноса 100 %; цвет Farrow & Ball No. 34			аналог по характеристикам	шт.	1		пом. 1
Т7	Портьеры-волна; лён 100 %; цвет NCS S 2010-Y30R; карниз 1820 мм, высота 2590 мм, сборка 2			аналог по характеристикам	шт.	2		пом. 3
Т8	Тюль; полиэстер 100 %; цвет Tikkurila V503; карниз 1820 мм, высота 2590 мм, сборка 2,5			аналог по характеристикам	шт.	1		пом. 3
Т9	Ковёр под кроватью; шерсть 100 %; цвет Farrow & Ball No. 66; 2500×1800 мм			аналог по характеристикам	шт.	1		пом. 3; с подложкой
Т10	Подушки декоративные на кровать; букле (шерсть 60 %, полиэстер 40 %); цвет Farrow & Ball No. 286			аналог по характеристикам	шт.	3		пом. 3
Т11	Подушки на кровать, акцент; хлопковый бархат 100 %; цвет NCS S 5030-B10G			аналог по характеристикам	шт.	2		пом. 3
Т12	Плед на кровать; шерсть мериноса 100 %; цвет Farrow & Ball No. 34			аналог по характеристикам	шт.	1		пом. 3
Т13	Портьеры-волна (гостиная); лён 70 %, вискоза 30 %; цвет NCS S 2010-Y30R; карниз 1650 мм, высота 2690 мм, сборка 2			аналог по характеристикам	шт.	2		пом. 4
Т14	Тюль (гостиная); полиэстер 100 %; цвет Tikkurila V503; карниз 1650 мм, высота 2690 мм, сборка 2,5			аналог по характеристикам	шт.	1		пом. 4
Т15	Римская штора (кухня); лён 100 %; цвет Farrow & Ball No. 66; карниз 1400 мм, высота 1700 мм			аналог по характеристикам	шт.	1		пом. 4
Т26	Римская штора (кухня, окно над рабочей зоной); лён 100 %; цвет Farrow & Ball No. 66; карниз 1000 мм, высота 1700 мм			аналог по характеристикам	шт.	1		пом. 4
Т16	Ковёр в зоне отдыха; шерсть 100 %; цвет Farrow & Ball No. 66; 3000×1150 мм			аналог по характеристикам	шт.	1		пом. 4; с подложкой
Т17	Подушки на диван; букле (шерсть 60 %, полиэстер 40 %); цвет NCS S 2010-Y30R			аналог по характеристикам	шт.	3		пом. 4
Т18	Подушки на диван, акцент; хлопковый бархат 100 %; цвет Farrow & Ball No. 34			аналог по характеристикам	шт.	2		пом. 4

Допущения и предложения на листе

Основа листа: размеры сняты с растрового плана заказчика с частичными размерами: рисунок не в масштабе, помещения выровнены по подписанным размерам мебели и проходов; контрольный обмер не выполнен (К-1); высота потолка 2700 мм принята: на плане заказчика её нет (К-2); толщины стен 300 / 120 мм приняты по плану заказчика, не замерены (К-1); разрешённая мощность 15 кВт принята по типовым ТУ для квартиры, ТУ заказчиком не переданы (К-4); подрайон климата не задан — принят не северный (жилые от 2,5 м) (К-6).

Знак «**» — предложение проектировщика, заказчиком не утверждено (согласовать с заказчиком): ИЗ-1: Т1, Т2 — Шина в нише штор (У1 +2,500, ниша +2,600 по всей стене А) — на окно 1 своя: 0…2300 по стене А (окно 500…2000: запас слева 500, справа 300 под пакет штор), вторая шина 2300…4600 — на окно 2 (Т27/Т28); вместе — длина ниши; Т27, Т28 — Шина на окно 2 в той же нише: 2300…4600 по стене А (окно 2600…4100: запас слева 300, справа 500); пара к Т1/Т2 на окне 1 — у обоих окон шторы, как на визуализации спальни; ИЗ-8: Кх6 — Остров сдвинут от кухонного ряда: торец острова стоял в 900 мм от фронта ПММ Кх3 и модуля Кх4 — меньше 1000 мм (СП 31-107-2004, п. 6.1.12) и меньше 1200 мм, при которых открытые ПММ и ящики не перекрывают проход.

См. лист открытых вопросов (лист 6, записи К-1, К-2, К-4, К-6; лист 7, запись ИЗ-1; лист 8, запись ИЗ-8).

Изм.	Кол.уч	Лист	№ док.	Подп.	Дата
Разраб.		Кырлан А.С.			04.11.26
Пров.					
ГИП					
Н. контр.					
Утв.					

ГД-2026-008-АИ

Квартира с кабинетом

Общая площадь 127,29* м² · * размеры со скана, не замерены (реестр — л. 6–8, К-1)

	Стадия	Лист	Листов
Дизайн-проект интерьера	РП	23	131

Спецификация мебели и оборудования (продолжение)
М б/м

Кырлан Александр Сергеевич

Спецификация мебели и оборудования (продолжение)

ПРЕДВАРИТЕЛЬНО · не для производства работ · открыто пунктов: 13 (реестр — л. 6–8)

Форма 1 ГОСТ 21.110-2013 · позиции мебели — по плану расстановки

Поз.	Наименование и техническая характеристика	Тип, марка, обозначение документа, опросного листа	Код продукции	Поставщик	Ед. измерения	Кол.	Масса 1 ед., кг	Примечание
Т19	Плед на диван; альпака 50 %, шерсть 50 %; цвет Farrow & Ball No. 66			аналог по характеристикам	шт.	1		пом. 4
Т20	Портьеры-волна; лён 100 %; цвет NCS S 2010-Y30R; карниз 1820 мм, высота 2590 мм, сборка 2			аналог по характеристикам	шт.	2		пом. 6
Т21	Тюль; полиэстер 100 %; цвет Tikkurila V503; карниз 1820 мм, высота 2590 мм, сборка 2,5			аналог по характеристикам	шт.	1		пом. 6
Т22**	Ковёр у кресла-кокона (зона чтения); шерсть 100 %; цвет Farrow & Ball No. 66; 1200×1700 мм			аналог по характеристикам	шт.	1		пом. 6; с подложкой
Т23	Подушки декоративные на кровать; букле (шерсть 60 %, полиэстер 40 %); цвет Farrow & Ball No. 286			аналог по характеристикам	шт.	3		пом. 6
Т24	Подушки на кровать, акцент; хлопковый бархат 100 %; цвет NCS S 5030-B10G			аналог по характеристикам	шт.	2		пом. 6
Т25	Плед на кровать; шерсть мериноса 100 %; цвет Farrow & Ball No. 34			аналог по характеристикам	шт.	1		пом. 6
	Декор							
ДК1	Картина над кроватью: абстракция, холст, тонкая рама из дуба; 1200×700 мм; низ на 1300 мм от пола			аналог по характеристикам	шт.	1	4	пом. 1; крепление к стене
ДК3	Картина над диваном: графика в паспарту, рама — дуб; 1400×700 мм; низ на 1000 мм от пола			аналог по характеристикам	шт.	1	4	пом. 3; крепление к стене
ДК4	Зеркало в рост в тонкой чёрной раме; рама — чёрный матовый; 600×1600 мм; низ на 300 мм от пола			аналог по характеристикам	шт.	1	12	пом. 3; крепление: анкер для пустотелых оснований, 4 шт.
ДК6	Картина: крупная абстракция в тёплой гамме, холст на подрамнике; 1200×900 мм; центр на 1550 мм от пола			аналог по характеристикам	шт.	1	6	пом. 4; крепление: анкер, 2 шт.
ДК7	Растение в кашпо; 450×450 мм			аналог по характеристикам	шт.	1		пом. 4
ДК8	Ваза керамическая с ветками на обеденном столе; 200×350 мм; на Кх8**			аналог по характеристикам	шт.	1		пом. 4
ДК2**	Картина над кроватью: графика в паспарту, рама — дуб; 600×700 мм; низ на 1200 мм от пола			аналог по характеристикам	шт.	1	4	пом. 6; крепление к стене
ДК5	Зеркало в рост в тонкой чёрной раме; рама — чёрный матовый; 600×1600 мм; низ на 300 мм от пола			аналог по характеристикам	шт.	1	12	пом. 6; крепление: анкер для пустотелых оснований, 4 шт.
ДК10**	Зеркало над умывальниками, влагостойкое, в тонкой латунной раме; 1400×700 мм; низ на 1200 мм от пола			аналог по характеристикам	шт.	1	12	пом. 7; крепление: клей для зеркал + 2 опорных уголка снизу, анкеры по основанию
ДК9	Зеркало; рама — чёрный матовый; 800×1800 мм; низ на 550 мм от пола			аналог по характеристикам	шт.	1	18	пом. 8; крепление: анкер, 4 шт.
ДК11**	Зеркало над умывальником, влагостойкое, в тонкой латунной раме; 500×700 мм; низ на 1200 мм от пола			аналог по характеристикам	шт.	1	5	пом. 9; крепление: клей для зеркал + 2 опорных уголка снизу

Допущения и предложения на листе

Основа листа: размеры сняты с растрового плана заказчика с частичными размерами: рисунок не в масштабе, помещения выровнены по подписанным размерам мебели и проходов; контрольный обмер не выполнен (К-1); высота потолка 2700 мм принята: на плане заказчика её нет (К-2); толщины стен 300 / 120 мм приняты по плану заказчика, не замерены (К-1); разрешённая мощность 15 кВт принята по типовым ТУ для квартиры, ТУ заказчиком не переданы (К-4); подрайон климата не задан — принят не северный (жилые от 2,5 м) (К-6).

Знак «**» — предложение проектировщика, заказчиком не утверждено (согласовать с заказчиком): ДК10 — Зеркало над умывальником — предмет света у зеркала (Св15 «настенный светильник над зеркалом») и место для лица у раковины; в данных его не было, светильник висел над сантехникой; ДК11 — Зеркало над умывальником — предмет света у зеркала (Св52 «настенный светильник над зеркалом») и место для лица у раковины; в данных его не было, светильник висел над сантехникой; ИЗ-1: Кх8 — 6 мест: банкетка Кх7 на 3 места и 3 стула (2 со свободной стороны, 1 у торца) вместо 6 стульев — со стороны банкетки стул не отодвинуть; Т22 — ковёр 1200 × 1700 у кресла-кокона вместо ковра 2500 × 1800 под кроватью: кровать в 520 мм от стены В, ковёр под ней не выходит за кровать на 450 мм и не оставляет 200 мм открытого пола у стены одновременно; ДК2 — низ 1200 = верх изголовья Дт2 1000 + 200 (150–250 над изголовьем, не над матрасом).

См. лист открытых вопросов (лист 6, записи К-1, К-2, К-4, К-6; лист 7, запись ИЗ-1).

Изм.	Кол.уч	Лист	№ док.	Подп.	Дата
Разраб.		Кырлан А.С.			04.11.26
Пров.					
ГИП					
Н. контр.					
Утв.					

ГД-2026-008-АИ

Квартира с кабинетом

Общая площадь 127,29* м² · * размеры со скана, не замерены (реестр — л. 6–8, К-1)

	Стадия	Лист	Листов
Дизайн-проект интерьера	РП	24	131
Спецификация мебели и оборудования (продолжение) М б/м	**Кырлан Александр Сергеевич**		

03

Электрооборудование


Кырлан Александр Сергеевич

выпуск 04.11.2026 № 4177cbe7a3 · стр. 27 из 166

План розеток и электровыводов

Розетки, выводы кабеля, щит · размеры в мм · высоты от чистого пола

ПРЕДВАРИТЕЛЬНО · не для производства работ · открыто пунктов: 13 (реестр — л. 6–8)

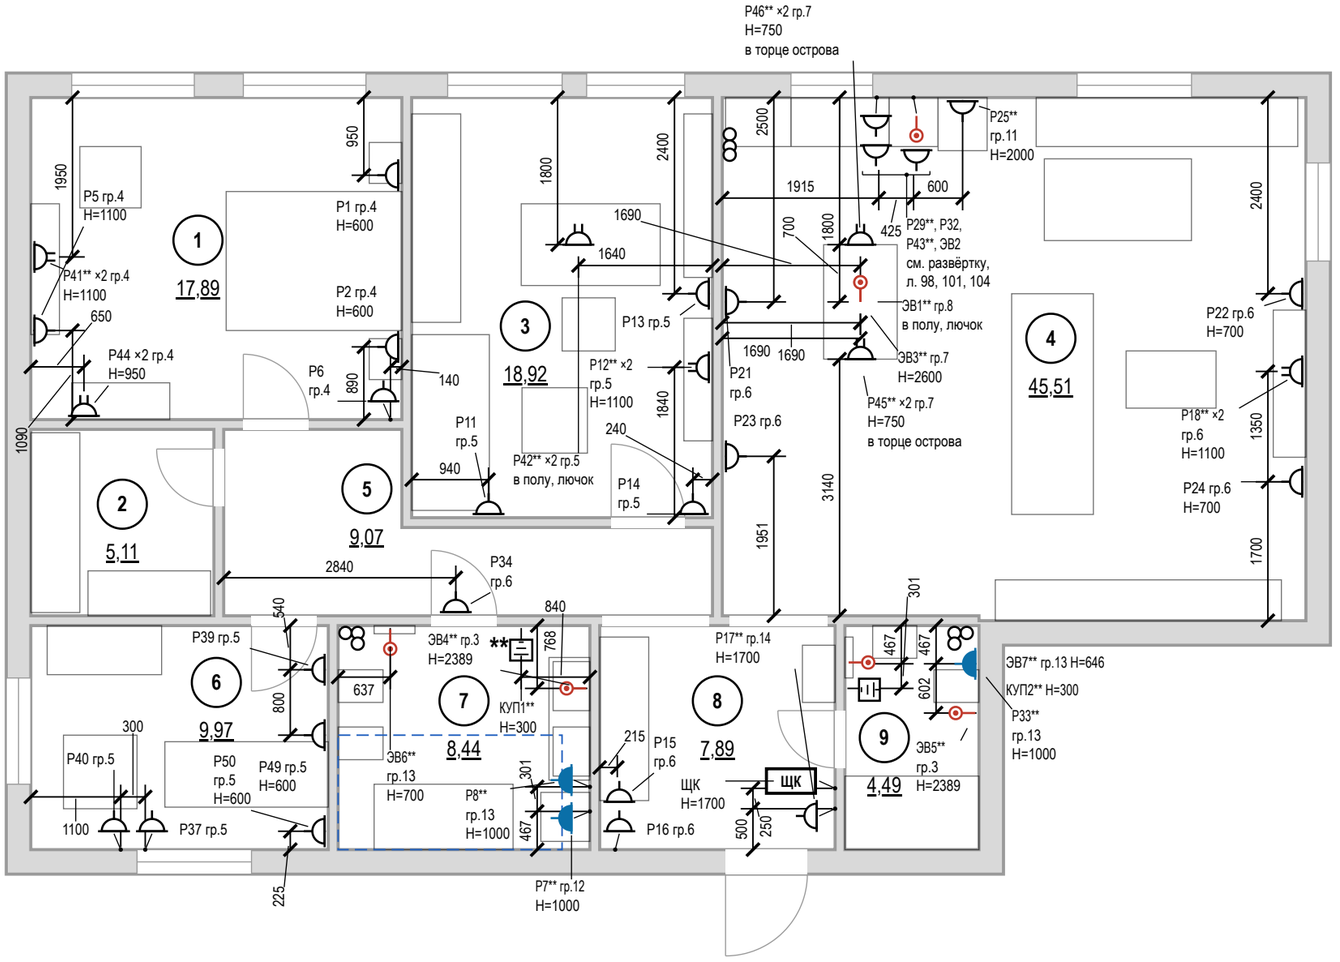

Условные обозначения

Знак	Тип изделия	H, мм	Кол., шт
	Розетка с заземлением	300	13
	То же	у знака	11
	Блок розеток с заземлением, рамка 2 поста	у знака	7
	Розетка с заземлением IP44	1000	3
	Вывод кабеля к прибору	у знака	7
	КУП (уравнивание потенциалов)	300	2
ЩК	Щит квартирный	1700	1

розетка с заземляющим контактом; у знака — марка, ×N — постов в рамке, гр. — группа щита, H — высота оси, мм

знак разведён для читаемости: точка на стене — у выноски, привязка — до неё

граница зоны 2 ванной (600 мм от ванны/поддона)

мебель и сантехприборы — подложка

стояк: К1 — канализация, В1 — ХВС, Т3 — ГВС

1 — номер помещения, площадь м²

Итого розеток (механизмов) — 41 шт; рамок — 34 шт: на 1 пост — 27, на 2 поста — 7.

Допущения и предложения на листе. Основа листа: размеры сняты с растрового плана заказчика с частичными размерами: рисунок не в масштабе, помещения выровнены по подписанным размерам мебели и проходов; контрольный обмер не выполнен (К-1); высота потолка 2700 мм принята: на плане заказчика её нет (К-2); толщины стен 300 / 120 мм приняты по плану заказчика, не замерены (К-1); разрешённая мощность 15 кВт принята по типовым ТУ для квартиры, ТУ заказчиком не переданы (К-4); подрайон климата не задан — принят не северный (жилые от 2,5 м) (К-6). Знак «**» — предложено, не утверждено (согласовать): P41, P12, P42, P18, P25, P29, ЭВ1, P43, P45, P46, P7, P8, ЭВ4, ЭВ6, P17, P33, ЭВ5, КУП2, ЭВ7; ИЗ-2: КУП1; ИЗ-8: ЭВ3. См. лист открытых вопросов (лист 6, записи К-1, К-2, К-4–К-6; лист 7, запись ИЗ-2; лист 8, запись ИЗ-8).

Примечания

1. За отметку 0,000 принят уровень чистого пола. Высоты H — от чистого пола до оси изделия; привязки — от чистовой грани стены до оси механизма (у рамки на несколько постов — до оси рамки).
2. Розетки без отметки H у знака — на высоте 300 мм от чистого пола до оси механизма; выводы кабеля — по паспорту прибора.
3. Розетки в санузле — только вне зон 0–2 (ПУЭ 7.1.48, ГОСТ Р 50571.7.701-2024), IP44, через УЗО 30 мА.
4. Розеточные и мокрые линии — через УЗО или дифавтомат с током утечки не более 30 мА (ПУЭ 7.1.79); в санузле выполнить ДСУП (ПУЭ 7.1.87–7.1.88).
5. Кабель — медный, исполнение нг(A)-LS (ГОСТ 31565-2012); скрытая прокладка только горизонтально и вертикально, фактические трассы зафиксировать исполнительной схемой до закрытия отделкой.
6. Расчёт нагрузок, токов КЗ, селективности и сечений — по проекту ЭОМ организации с допуском СРО; лист задаёт состав, расположение и группы.
7. Выводы кухонной техники — после утверждения проекта кухни (ориентировочно); привязки выводов даны от осей модулей гарнитура и пересматриваются вместе с проектом кухни.
8. Электрический тёплый пол проектом не предусмотрен; при решении заказчика устроить — отдельный лист «План тёплых полов»: контуры с отступом 100 мм от стен и мебели без ножек, датчик в гофре, терморегулятор, своя группа щита через УЗО 30 мА.
9. Ведомости электроточек, изделий, светильников и расшифровка клавиш — лист 28.

1000 мм · печать 1:1

Изм.	Кол.уч	Лист	№ док.	Подп.	Дата
Разраб.		Кырлан А.С.			04.11.26
Пров.					
ГИП					
Н. контр.					
Утв.					

ГД-2026-008-АИ

Квартира с кабинетом

Общая площадь 127,29* м² · * размеры со скана, не замерены (реестр — л. 6–8, К-1)

Дизайн-проект интерьера

Стадия	Лист	Листов
РП	25	131


План розеток и электровыводов

М 1:75

Кырлан Александр Сергеевич

План освещения

Светильники, группы включения, извещатели · размеры в мм

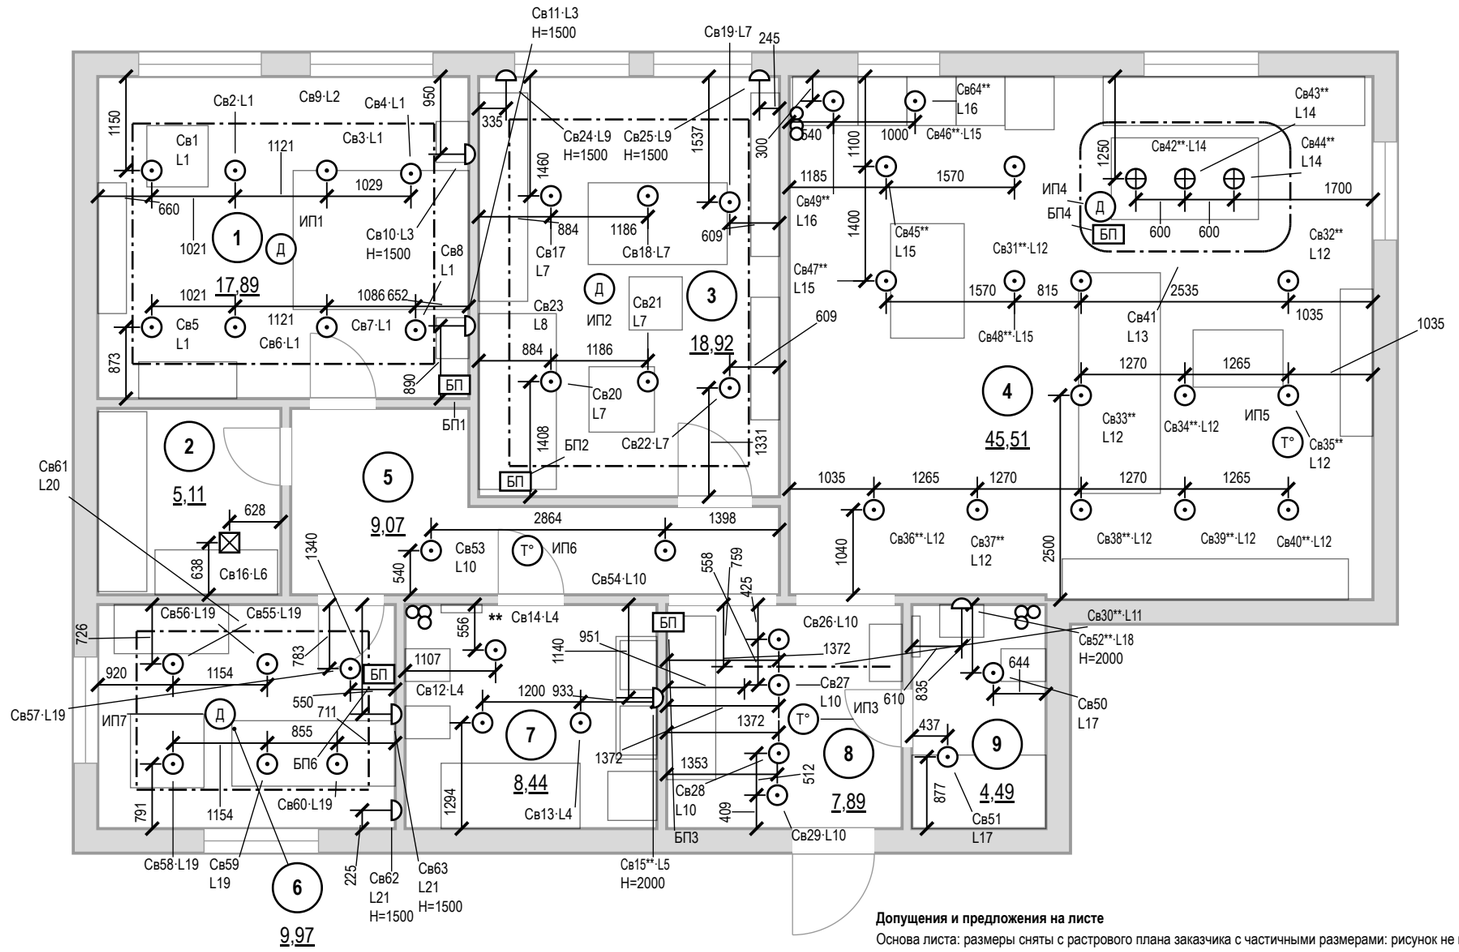

Условные обозначения

- светильник встраиваемый точечный
- светильник потолочный накладной
- светильник подвесной
- светильник настенный (бра), H — высота оси
- светодиодная лента в профиле / в карнизе короба
- Св1·L1 — марка светильника (как в ведомости и на развёртках) · группа включения L (лист 27)
- Д — извещатель пожарный дымовой автономный
- Т° — извещатель пожарный тепловой
- БП — блок питания LED, с доступом (люк от 100×100 мм)
- мебель и сантехприборы — подложка
- стояк: К1 — канализация, В1 — ХВС, Т3 — ГВС
- 1 — номер помещения, площадь м²

Допущения и предложения на листе

Основа листа: размеры сняты с растрового плана заказчика с частичными размерами: рисунок не в масштабе, помещения выровнены по подписанным размерам мебели и проходов; контрольный обмер не выполнен (К-1); высота потолка 2700 мм принята: на плане заказчика её нет (К-2); толщины стен 300 / 120 мм приняты по плану заказчика, не замерены (К-1); разрешённая мощность 15 кВт принята по типовым ТУ для квартиры, ТУ заказчиком не переданы (К-4); подрайон климата не задан — принят не северный (жилые от 2,5 м) (К-6).

Знак «**» — предложение проектировщика, заказчиком не утверждено (согласовать с заказчиком): Св31, Св32, Св33, Св34, Св35, Св36, Св37, Св38, Св39, Св40 — ряды — по зоне гостиной (по мебели); Св42, Св43, Св44 — диммируемость добавлена разработчиком проекта под светорегуляторы S9 и S10; Св45, Св46, Св47, Св48 — ряды — по зоне кухни (по мебели); Св49, Св64 — навесных шкафов на кухне нет: рабочий свет столешницы — потолочные светильники над столешницей (ряд по середине её глубины) (линейную подсветку «под шкафами» крепить не к чему); параметры — для подбора; диммируемость добавлена разработчиком проекта под светорегуляторы S9 и S10; Св15, Св52 — свет у зеркала — над зеркалом у умывальника по его оси (свет на лицо, а не над сантехникой); Св30 — открытая лента в накладном профиле вместо «в коробе»: короба в потолке нет — подвесной потолок помещения без короба и ниши LED; ИЗ-2, К-5: дверь пом. 7 (стена А) — Проём сдвинут вдоль стены А от угла Б: offset 2300 → 1200 — утверждено автором (ИЗ-2, Кырлан А.С.).

См. лист открытых вопросов (лист 6, записи К-1, К-2, К-4–К-6; лист 7, запись ИЗ-2).

Примечания

1. За отметку 0,000 принят уровень чистого пола. Высоты H — от чистого пола до оси изделия; привязки — от чистовой грани стены до оси механизма (у рамки на несколько постов — до оси рамки).
2. Высота установки, не указанная на плане: светильники — на потолке; настенные — по отметке H у знака. Привязки — до оси светильника от чистовой грани стены, по рядам.
3. Во влажных помещениях — светильники не ниже IP44; в зонах 0–2 ванной — по ГОСТ Р 50571.7.701-2024 (зона 1 — IPX5).
4. LED-лента в карнизе подсветки короба — по линии карниза с плана потолков; блок питания — в люке короба (БП на плане), питание ленты длиннее 5 м — с двух концов.
5. Розеточные и мокрые линии — через УЗО или дифавтомат с током утечки не более 30 мА (ПУЭ 7.1.79); в санузле выполнить ДСУП (ПУЭ 7.1.87–7.1.88).
6. Кабель — медный, исполнение нг(A)-LS (ГОСТ 31565-2012); скрытая прокладка только горизонтально и вертикально, фактические трассы зафиксировать исполнительной схемой до закрытия отделкой.
7. Расчёт нагрузок, токов КЗ, селективности и сечений — по проекту ЭОМ организации с допуском СРО; лист задаёт состав, расположение и группы.
8. Ведомость светильников (тип, количество, мощность, поток, Тц, Ra) — лист 47.
9. Оценка освещённости (по норме СанПиН 1.2.3685-21, табл. 5.52, на полу; не светотехнический расчёт, декоративная подсветка в оценку не входит) — лист 28.

1000 мм · печать 1:1

Изм.	Кол.уч	Лист	№ док.	Подп.	Дата
Разраб.		Кырлан А.С.			04.11.26
Пров.					
ГИП					
Н. контр.					
Утв.					

ГД-2026-008-АИ

Квартира с кабинетом

Общая площадь 127,29* м² · * размеры со скана, не замерены (реестр — л. 6–8, К-1)

Дизайн-проект интерьера

Стадия	Лист	Листов
РП	26	131

План освещения

М 1:75


Кырлан Александр Сергеевич

выпуск 04.11.2026 № 4177cbe7a3 · стр. 29 из 166

План выключателей и схема включения

Выключатели S, группы включения L, линии связи · размеры в мм

ПРЕДВАРИТЕЛЬНО · не для производства работ · открыто пунктов: 13 (реестр — л. 6–8)

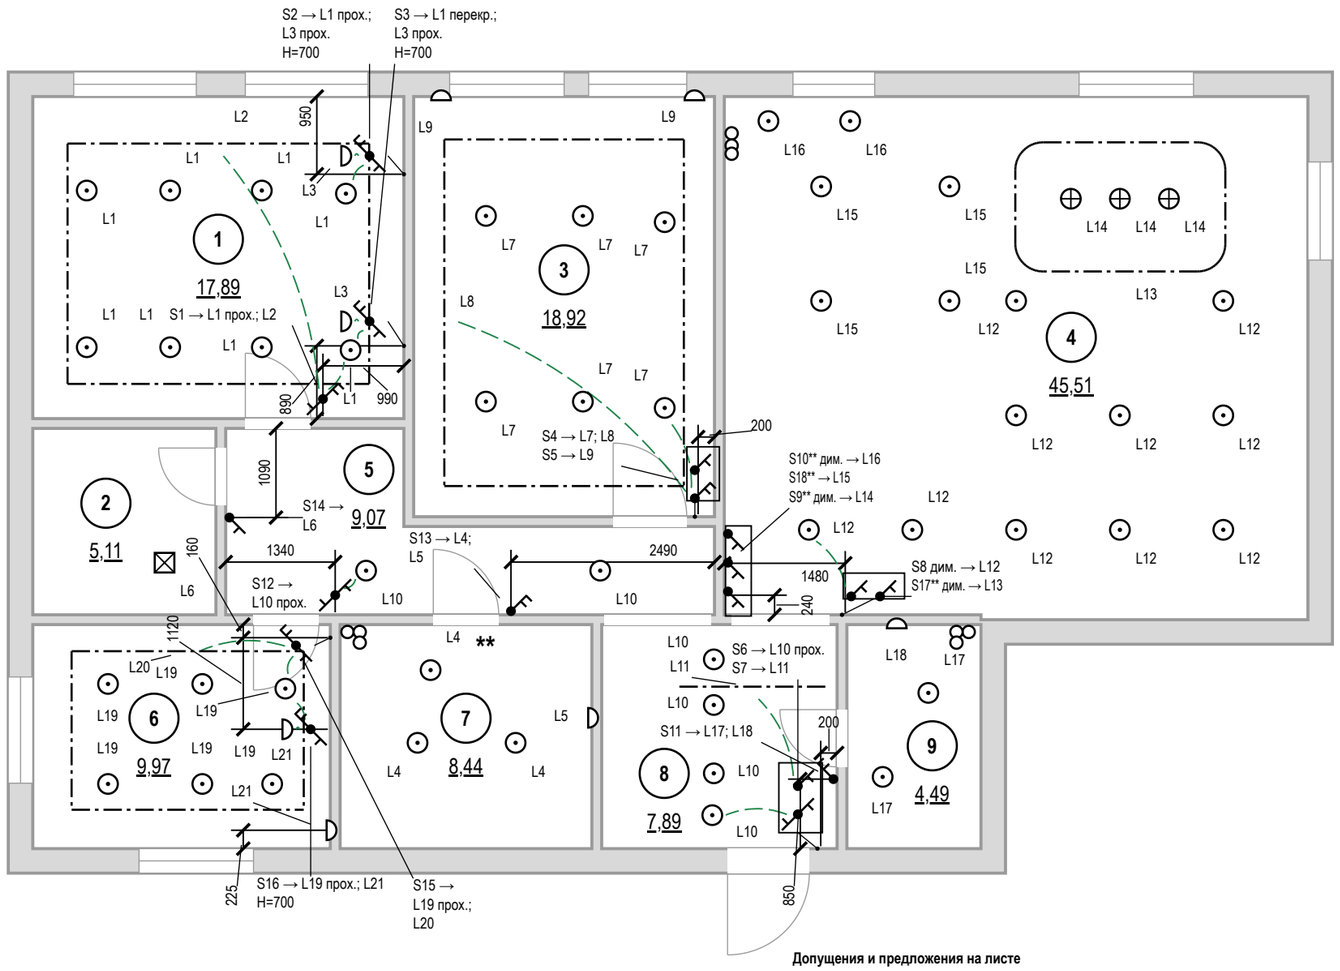

Условные обозначения

- выключатель одноклавишный
- выключатель двухклавишный (флажков — по числу клавиш)
- выключатель с проходной или перекрёстной клавишей (обратный флажок); тип клавиши — в подписи
- S1 → — марка → группы по клавишам (через «;»): прох. — проходной, перекр. — перекрёстный, дим. — светорегулятор; Н — высота
- связь: выключатель → ближайший светильник группы в том же помещении (не трасса кабеля); полный состав группы — по номеру L
- светильник встраиваемый точечный
- светильник потолочный накладной
- светильник подвесной
- светильник настенный (бра), Н — высота оси
- светодиодная лента в профиле / в карнизе короба
- L1 — группа включения у светильника
- стояк: К1 — канализация, В1 — ХВС, Т3 — ГВС
- 1 — номер помещения, площадь м²

Допущения и предложения на листе

Основа листа: размеры сняты с растрового плана заказчика с частичными размерами: рисунок не в масштабе, помещения выровнены по подписанным размерам мебели и проходов; контрольный обмер не выполнен (К-1); высота потолка 2700 мм принята: на плане заказчика её нет (К-2); толщины стен 300 / 120 мм приняты по плану заказчика, не замерены (К-1); разрешённая мощность 15 кВт принята по типовым ТУ для квартиры, ТУ заказчиком не переданы (К-4); подрайон климата не задан — принят не северный (жилые от 2,5 м) (К-6).

Знак «**» — предложение проектировщика, заказчиком не утверждено (согласовать с заказчиком): S17 — свой пост группе L13: сценарии «Вечер», «Ужин», «Кино», «Готовка» включают её отдельно от L12 — на одном светорегуляторе не набрать; S9, S10 — светорегулятор добавлен разработчиком проекта; S18 — свой пост группе L15: сценарии «Вечер», «Ужин», «Готовка» включают её отдельно от L14 — на одном светорегуляторе не набрать; ИЗ-2, К-5: дверь пом. 7 (стена А) — Проём сдвинут вдоль стены А от угла Б: offset 2300 → 1200 — утверждено автором (ИЗ-2, Кырлан А.С.).

См. лист открытых вопросов (лист 6, записи К-1, К-2, К-4–К-6; лист 7, запись ИЗ-2).

Примечания

1. За отметку 0,000 принят уровень чистого пола. Высоты Н — от чистого пола до оси изделия; привязки — от чистовой грани стены до оси механизма (у рамки на несколько постов — до оси рамки).
2. Высота установки, не указанная на плане: выключатели — 900 мм от чистого пола (у кровати и другие — Н у марки), со стороны дверной ручки (ПУЭ 7.1.51).
3. Какой выключатель какие светильники включает — по номеру группы L: у выключателя (S1 → L1; L2 — клавиши по порядку) и у каждого светильника. Пунктир подсказка к ближайшему светильнику группы в том же помещении (не дальше 3 м), это не трасса кабеля; выключатель за стеной (у двери санузла) и далёкая группа — только номер группы.
4. Группы из нескольких мест (L1 — S1, S2, S3; L3 — S2, S3; L10 — S6, S12; L19 — S15, S16): на крайних местах — проходные клавиши, на промежуточных перекрёстные; механизмы — в ведомости изделий.
5. Светорегулятор — по заднему фронту (для LED-драйверов), совместимость с драйверами проверить до закупки.
6. Розеточные и мокрые линии — через УЗО или дифавтомат с током утечки не более 30 мА (ПУЭ 7.1.79); в санузле выполнить ДСУП (ПУЭ 7.1.87–7.1.88).
7. Кабель — медный, исполнение нг(А)-LS (ГОСТ 31565-2012); скрытая прокладка только горизонтально и вертикально, фактические трассы зафиксировать исполнительной схемой до закрытия отделкой.
8. Расчёт нагрузок, токов КЗ, селективности и сечений — по проекту ЭОМ организации с допуском СРО; лист задаёт состав, расположение и группы.
9. Расшифровка клавиш и ведомость изделий — лист 28.

1000 мм · печать 1:1

Изм.	Кол.уч	Лист	№ док.	Подп.	Дата
Разраб.		Кырлан А.С.			04.11.26
Пров.					
ГИП					
Н. контр.					
Утв.					

ГД-2026-008-АИ

Квартира с кабинетом

Общая площадь 127,29* м² · * размеры со скана, не замерены (реестр — л. 6–8, К-1)

Дизайн-проект интерьера

Стадия	Лист	Листов
РП	27	131

План выключателей и схема включения

М 1:75

Кырлан Александр Сергеевич

выпуск 04.11.2026 № 4177cbe7a3 · стр. 30 из 166

Ведомость электроточек и изделий

Электроточки, изделия, светильники, освещённость, клавиши выключателей · б/м

Ведомость электроточек

Марка	Пом.	Назначение	Н, мм	Гр.
Р1	1	у кровати	600	4
Р2	1	у кровати	600	4
Р5	1	торшер у кресла	1100	4
Р6	1	уборка	300	4
Р41**	1	ТВ-зона: питание ТВ и приставки	1100	4
Р44	1	туалетный столик: фен, подсветка зеркала	950	4
Р11	3	общего назначения	300	5
Р12**	3	ТВ-зона: питание ТВ и приставки	1100	5
Р13	3	уборка	300	5
Р14	3	уборка у входа	300	5
Р42**	3	рабочий стол — лючок в полу под столом	0	5
Р18**	4	ТВ-зона: питание ТВ и приставки	1100	6
Р21	4	общего назначения	300	6
Р22	4	общего назначения	700	6
Р23	4	уборка, пылесос	300	6
Р24	4	общего назначения	700	6
Р25**	4	холодильник — над нишей, съёмная панель	2000	11
Р29**	4	фартук	1200	7
Р32	4	посудомоечная машина — в соседнем модуле, за ящиком	300	10
Р43**	4	СВЧ — над нишей, съёмная панель	1960	7
Р45**	4	столешница острова — в торцевой панели	750	7
Р46**	4	столешница острова — в торцевой панели	750	7
ЭВ1**	4	варочная панель на острове вывод из пола под островом, в цоколе	0	8
ЭВ2	4	духовой шкаф — в цоколе	150	9
ЭВ3**	4	вытяжка островная — вывод на потолке над островом (клеммная коробка в закладной)	2600	7
Р34	5	уборка	300	6

Ведомость электроточек (продолжение)

Марка	Пом.	Назначение	Н, мм	Гр.
Р37	6	общего назначения	300	5
Р39	6	уборка	300	5
Р40	6	уборка	300	5
Р49	6	у кровати	600	5
Р50	6	у кровати	600	5
КУП1**	7	КУП — уравнивание потенциалов (ДСУП)	300	
Р7**	7	стиральная машина, IP44	1000	12
Р8**	7	фен у умывальника, IP44	1000	13
ЭВ4**	7	вентилятор ВР1 (таймер выбега)	2389	3
ЭВ6**	7	полотенцесушитель П7, IP44	700	13
Р15	8	пылесос, сушилка обуви	300	6
Р16	8	уборка	300	6
Р17**	8	питание слаботочного щита (рядом с ЩС**)	1700	14
ЩК	8	щит квартирный ЩРВ-П-48	1700	
КУП2**	9	КУП — уравнивание потенциалов (ДСУП)	300	
Р33**	9	фен у умывальника, IP44	1000	13
ЭВ5**	9	вентилятор ВР3 (таймер выбега)	2389	3
ЭВ7**	9	полотенцесушитель П13**, IP44	646	13

Ведомость изделий

Наименование	Марки	Ед.	Кол.
Розетка с з/к и защитными шторками, 16 А	по ведомости точек	шт	38
Розетка IP44 с крышкой, 16 А	Р7**, Р8**, Р33**	шт	3
Выключатель 1-клав.	S5, S7, S14, S18**	шт	4
Выключатель 1-клав. проходной	S6, S12	шт	2
Выключатель 2-клав.	S4, S11, S13	шт	3
Выключатель 2-клав. (перекрёстная + проходная)	S3	шт	1
Выключатель 2-клав. (проходная + обычная)	S1, S15, S16	шт	3
Выключатель 2-клав. проходной	S2	шт	1
Светорегулятор 1-канальный, задний фронт (LED)	S8, S9**, S10**, S17**	шт	4
Датчик движения ночной подсветки	L11	шт	1

Ведомость изделий (продолжение)

Наименование	Марки	Ед.	Кол.
Рамка 1-постовая	в т. ч. 18 под выключ.	шт	45
Рамка 2-постовая		шт	7
Коробка установочная (подрозетник) Ø68	розетки, выключатели	шт	59
Вывод кабеля под прибор (клеммник)	ЭВ1**, ЭВ2, ЭВ3**, ЭВ4**, ЭВ5**, ЭВ6**, ЭВ7**	шт	7
Коробка уравнивания потенциалов КУП	КУП1**, КУП2**	шт	2
Блок питания LED 24 В, 200 Вт, дим.	БП1, БП2, БП6	шт	3
Блок питания LED 24 В, 300 Вт, дим.	БП4	шт	1
Блок питания LED 24 В, 20 Вт	БП3	шт	1
Извещатель дымовой автономный	ИП1, ИП2, ИП4, ИП7	шт	4
Извещатель тепловой	ИП3, ИП5, ИП6	шт	3
Щит квартирный (состав — лист щита)	ЩК	шт	1
Розетка компьютерная RJ45, кат. 6, с рамкой и подрозетником	LAN2–LAN5, LAN6**	шт	5
Розетка телевизионная (коаксиальная) с рамкой и подрозетником	ТВ1, ТВ2, ТВ4	шт	3
Точка доступа Wi-Fi (оборудование заказчика), питание PoE	АР1**, АР2**	шт	2
Трубка или монитор домофона (поставка домофонной организации)	ДФ1	шт	1
Щит слаботочный ЩС**: корпус, DIN-рейка, розетки 220 В	ЩС**	шт	1
Патч-панель, портов не менее 7		шт	1
Коммутатор, портов не менее 7, из них PoE 2		шт	1
Кабель домофона — тип по системе поставщика (по лучам от ЩС**, запас 10 %)		м	5,7
Кабель коаксиальный RG-6 (75 Ом) к розеткам ТВ (по лучам от ЩС**, запас 10 %)		м	57
Кабель U/UTP кат. 6 (LAN, Wi-Fi и камеры по PoE) (по лучам от ЩС**, запас 10 %)		м	110,6

Ведомость светильников

Поз.	Марки	Тип	Кол.	Р, Вт	Ф, лм	IP	Тц/Ra
1	Св1–Св8	встраиваемый точечный	8	12	1000		2700/90
2	Св9	светодиодная лента, 13,3 м	1	127,7	11970		2700/90
3	Св10, Св11, Св24, Св25, Св62, Св63	настенный (бра), Н=1500	6	6	400		2700/90
4	Св16	потолочный накладной	1	10	900		3000/90
5	Св17–Св22, Св55–Св60	встраиваемый точечный	12	12	1050		2700/90
6	Св23	светодиодная лента, 14,3 м	1	137,3	12870		2700/90
7	Св31**, Св32**, Св33**, Св34**, Св35**, Св36**, Св37**, Св38**, Св39**, Св40**	встраиваемый точечный	10	12	1000		3000/90
8	Св41	светодиодная лента, 7,7 м	1	73,9	6930		2700/90
9	Св42**, Св43**, Св44**	подвесной	3	9	800		3000/90
10	Св45**, Св46**, Св47**, Св48**	встраиваемый точечный	4	10	900		3000/90
11	Св26–Св29, Св49**, Св53, Св54, Св64**	встраиваемый точечный	8	7	600		3000/90
12	Св61	светодиодная лента, 9,6 м	1	92,2	8640		2700/90
13	Св12–Св14, Св51	встраиваемый точечный	4	6	500	44	3000/90
14	Св15**, Св52**	настенный (бра), Н=2000	2	8	600	44	3000/90
15	Св30**	светодиодная лента, 1,8 м	1	8,6	270		2700/90
16	Св50	встраиваемый точечный	1	7	600	44	3000/90

Примечания

1. Ведомости сведены с планов розеток, освещения и выключателей; марки, группы и высоты — те же, что у знаков на планах.
2. Механизмы, рамки и светорегуляторы — одной серии; число постов и клавиш сверено с выбранной серией. Перекрёстная клавиша — отдельный механизм серии.
3. Освещённость (оценка) — по норме СанПиН 1.2.3685-21 (табл. 5.52, на полу), не светотехнический расчёт; декоративная подсветка в оценку не входит.
4. За отметку 0,000 принят уровень чистого пола. Высоты Н — от чистого пола до оси изделия; привязки — от чистовой грани стены до оси механизма (у рамки на несколько постов — до оси рамки).
5. Розеточные и мокрые линии — через УЗО или дифавтомат с током утечки не более 30 мА (ПУЭ 7.1.79); в санузле выполнить ДСУП (ПУЭ 7.1.87–7.1.88).
6. Кабель — медный, исполнение нг(А)-LS (ГОСТ 31565-2012); скрытая прокладка только горизонтально и вертикально, фактические трассы зафиксировать исполнительной схемой до закрытия отделкой.
7. Расчёт нагрузок, токов КЗ, селективности и сечений — по проекту ЭОМ организации с допуском СРО; лист задаёт состав, расположение и группы.
8. Ведомости занимают 2 листов этого наименования: таблицы, не вошедшие в поле листа, продолжены на следующем листе.

Допущения и предложения на листе. Знак «**» предложено (согласовать). См. лист открытых вопросов (листы 6–8).

Изм.	Кол.уч	Лист	№ док.	Подп.	Дата
Разраб.		Кырлан А.С.			04.11.26
Пров.					
ГИП					
Н. контр.					
Утв.					

ГД-2026-008-АИ

Квартира с кабинетом

Общая площадь 127,29* м² · * размеры со скана, не замерены (реестр — л. 6–8, К-1)

Дизайн-проект интерьера

Стадия	Лист	Листов
РП	28	131

Ведомость электроточек и изделий

М б/м

Кырлан Александр Сергеевич

выпуск 04.11.2026 № 4177cbe7a3 · стр. 31 из 166

Ведомость электроточек и изделий (продолжение)

Электроточки, изделия, светильники, освещённость, клавиши выключателей · б/м

Освещённость (оценка)

Пом.	S, м²	Ен, лк	Ф треб., лм	Ф по пр., лм
1	17,9	150	7560	8000
2	5,1	75	1080	900
3	18,9	300	15990	6300
4	45,5	150	19230	16000
5	9,1	50	1280	1200
6	10	200	5620	6300
7	8,4	50	1190	1500
8	7,9	50	1110	2400
9	4,5	50	630	1100

Расшифровка клавиш

Марка	Пом.	Н, мм	Клав.	Механизм	Группа: светильники
S1	1	900	1	проходной	L1: Св1–Св8
			2	обычный	L2: Св9
S2	1	700	1	проходной	L1: Св1–Св8
			2	проходной	L3: Св10, Св11
S3	1	700	1	перекрёстный	L1: Св1–Св8
			2	проходной	L3: Св10, Св11
S4	3	900	1	обычный	L7: Св17–Св22
			2	обычный	L8: Св23
S5	3	900	1	обычный	L9: Св24, Св25
S6	8	900	1	проходной	L10: Св26–Св29, Св53, Св54
S7	8	900	1	обычный	L11: Св30**
S8	4	900	1	светорегулятор	L12: Св31**, Св32**, Св33**, Св34**, Св35**, Св36**, Св37**, Св38**, Св39**, Св40**
S9**	4	900	1	светорегулятор	L14: Св42**, Св43**, Св44**
S10**	4	900	1	светорегулятор	L16: Св49**, Св64**
S11	8	900	1	обычный	L17: Св50, Св51
			2	обычный	L18: Св52**
S12	5	900	1	проходной	L10: Св26–Св29, Св53, Св54
S13	5	900	1	обычный	L4: Св12–Св14
			2	обычный	L5: Св15**

Расшифровка клавиш (продолжение)

Марка	Пом.	Н, мм	Клав.	Механизм	Группа: светильники
S14	5	900	1	обычный	L6: Св16
S15	6	900	1	проходной	L19: Св55–Св60
			2	обычный	L20: Св61
S16	6	700	1	проходной	L19: Св55–Св60
			2	обычный	L21: Св62, Св63
S17**	4	900	1	светорегулятор	L13: Св41
S18**	4	900	1	обычный	L15: Св45**, Св46**, Св47**, Св48**

Допущения и предложения на листе

Основа листа: размеры сняты с растрового плана заказчика с частичными размерами: рисунок не в масштабе, помещения выровнены по подписанным размерам мебели и проходов; контрольный обмер не выполнен (К-1); высота потолка 2700 мм принята: на плане заказчика её нет (К-2); толщины стен 300 / 120 мм приняты по плану заказчика, не замерены (К-1); разрешённая мощность 15 кВт принята по типовым ТУ для квартиры, ТУ заказчиком не переданы (К-4); подрайон климата не задан — принят не северный (жилые от 2,5 м) (К-6).

Знак «**» — предложение проектировщика, заказчиком не утверждено (согласовать с заказчиком): S17 — свой пост группе L13: сценарии «Вечер», «Ужин», «Кино», «Готовка» включают её отдельно от L12 — на одном светорегуляторе не набрать; S9, S10 — светорегулятор добавлен разработчиком проекта; S18 — свой пост группе L15: сценарии «Вечер», «Ужин», «Готовка» включают её отдельно от L14 — на одном светорегуляторе не набрать; Св31, Св32, Св33, Св34, Св35, Св36, Св37, Св38, Св39, Св40 — ряды — по зоне гостиной (по мебели); Св42, Св43, Св44 — диммируемость добавлена разработчиком проекта под светорегуляторы S9 и S10; Св45, Св46, Св47, Св48 — ряды — по зоне кухни (по мебели); Св49, Св64 — навесных шкафов на кухне нет: рабочий свет столешницы — потолочные светильники над столешницей (ряд по середине её глубины) (линейную подсветку «под шкафами» крепить не к чему); параметры — для подбора; диммируемость добавлена разработчиком проекта под светорегуляторы S9 и S10; Св15, Св52 — свет у зеркала — над зеркалом у умывальника по его оси (свет на лицо, а не над сантехникой); Св30 — открытая лента в накладном профиле вместо «в коробе»: короба в потолке нет — подвесной потолок помещения без короба и ниши LED.

См. лист открытых вопросов (лист 6, записи К-1, К-2, К-4, К-6).

Примечания

1. Продолжение ведомостей: лист 2 из 2 этого наименования; таблицы, прерванные на предыдущем листе, продолжены с заголовком «(продолжение)».
2. За отметку 0,000 принят уровень чистого пола. Высоты Н — от чистого пола до оси изделия; привязки — от чистовой грани стены до оси механизма (у рамки на несколько постов — до оси рамки).
3. Розеточные и мокрые линии — через УЗО или дифавтомат с током утечки не более 30 мА (ПУЭ 7.1.79); в санузле выполнить ДСУП (ПУЭ 7.1.87–7.1.88).
4. Кабель — медный, исполнение нг(А)-LS (ГОСТ 31565-2012); скрытая прокладка только горизонтально и вертикально, фактические трассы зафиксировать исполнительной схемой до закрытия отделкой.
5. Расчёт нагрузок, токов КЗ, селективности и сечений — по проекту ЭОМ организации с допуском СРО; лист задаёт состав, расположение и группы.

Изм.	Кол.уч	Лист	№ док.	Подп.	Дата
Разраб.		Кырлан А.С.			04.11.26
Пров.					
ГИП					
Н. контр.					
Утв.					

ГД-2026-008-АИ

Квартира с кабинетом

Общая площадь 127,29* м² · * размеры со скана, не замерены (реестр — л. 6–8, К-1)

Дизайн-проект интерьера

Стадия	Лист	Листов
РП	29	131


Ведомость электроточек и изделий (продолжение)

М б/м

Кырлан Александр Сергеевич

Однолинейная схема щита

Щит квартирный ЩК · гр. 1—14 из 14 · без масштаба

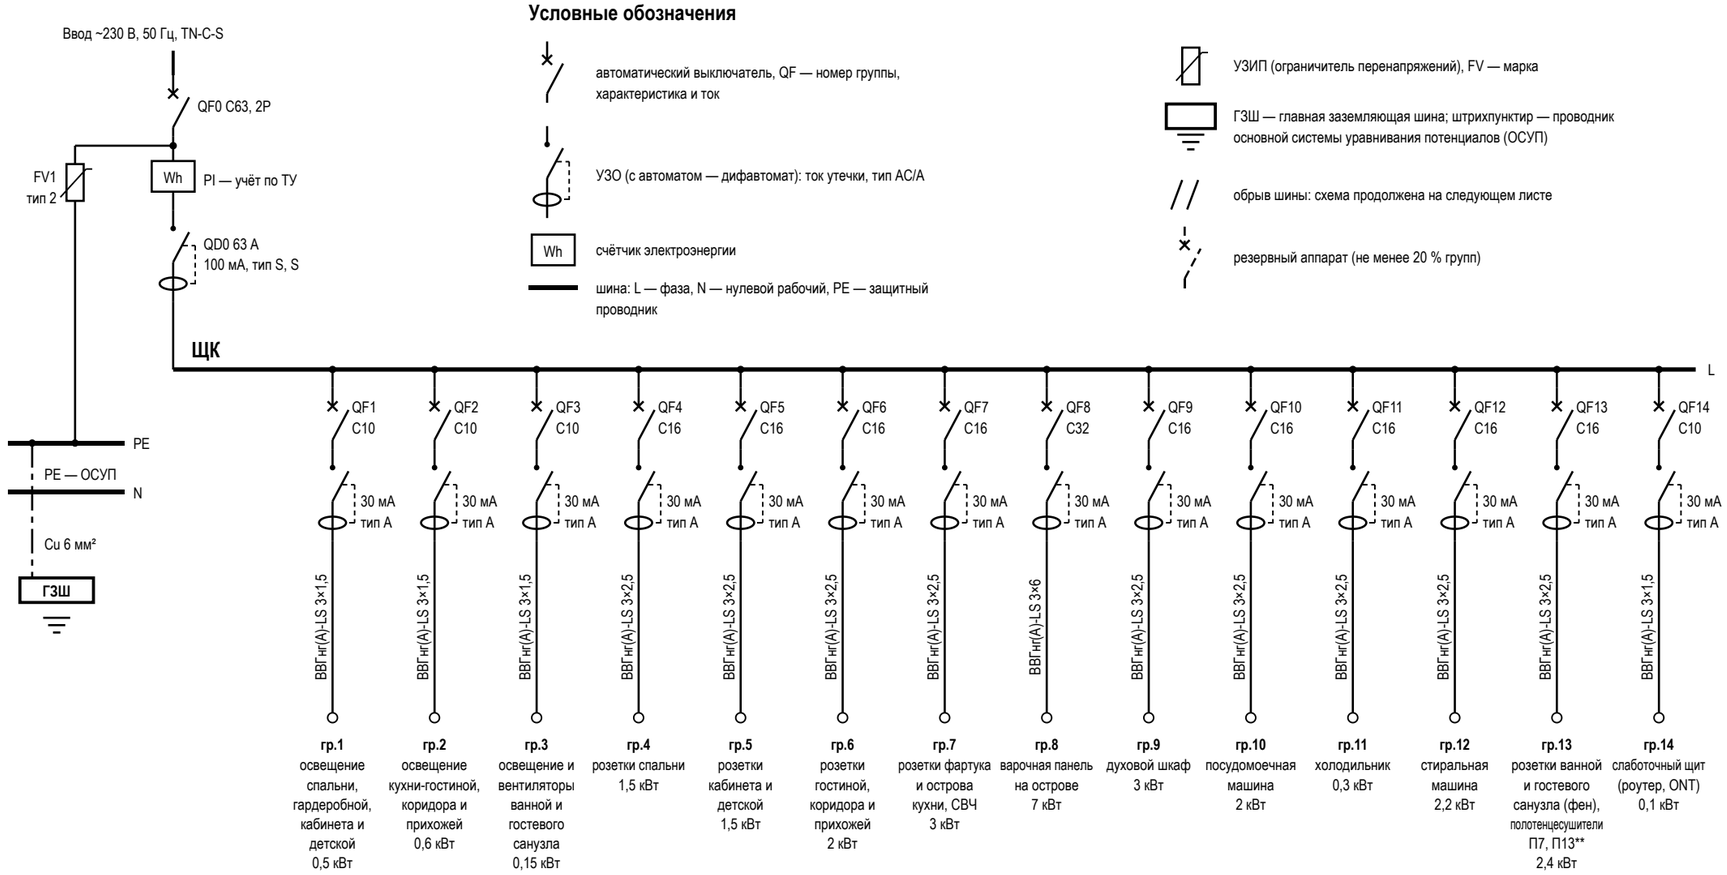

Условные обозначения

- автоматический выключатель, QF — номер группы, характеристика и ток
- УЗО (с автоматом — дифавтомат): ток утечки, тип AC/A
- Wh — счётчик электроэнергии
- шина: L — фаза, N — нулевой рабочий, PE — защитный проводник
- УЗИП (ограничитель перенапряжений), FV — марка
- ГЗШ — главная заземляющая шина; штрихпунктир — проводник основной системы уравнивания потенциалов (ОСУП)
- обрыв шины: схема продолжена на следующем листе
- резервный аппарат (не менее 20 % групп)

Данные щитка

Показатель	Значение
Номер щитка	ЩК
Тип	ЩРВ-П-48, IP41
Уст. мощность, кВт	26,25
Разреш. мощность, кВт	15
Расчётная, кВт	9,8
Автоматы 1п: занят. / рез.	14 / 3
Модулей: всего / занято	48 / 34
Ток на вводе, А	63
Вводной аппарат	QF0 C63, 2P
УЗИП	FV1, тип 2, ЩК, после счётчика
ГЗШ, проводник ОСУП	Cu 6 мм²
Листов схемы	2 (группы по листам)

Допущения и предложения на листе

Основа листа: размеры сняты с растрового плана заказчика с частичными размерами: рисунок не в масштабе, помещения выровнены по подписанным размерам мебели и проходов; контрольный обмер не выполнен (К-1); высота потолка 2700 мм принята: на плане заказчика её нет (К-2); толщины стен 300 / 120 мм приняты по плану заказчика, не замерены (К-1); разрешённая мощность 15 кВт принята по типовым ТУ для квартиры, ТУ заказчиком не переданы (К-4); подрайон климата не задан — принят не северный (жилые от 2,5 м) (К-6).

Знак «**» — предложение проектировщика, заказчиком не утверждено (согласовать с заказчиком): П13 — Полотенцесушитель — по образцу (как П7 в ванной): прибор отопления мокрой зоны; вывод ЭВ7 электрика под него уже стоял, а прибора в данных ВК не было — лист выводов и ЭОМ расходились.

Открытые вопросы и конфликты по листу: К-4.

См. лист открытых вопросов (лист 6, записи К-1, К-2, К-4, К-6).

Таблица групп щита ЩК и кабельный журнал

№	Назначение	Помещения	Автомат	УЗО / дифавтомат	Кабель	Длина, м	P, кВт	Точек
1	освещение спальни, гардеробной, кабинета и детской	1, 2, 3, 5, 6	C10	30 мА, тип A	ВВГнг(A)-LS 3×1,5	123,1	0,5	41
2	освещение кухни-гостиной, коридора и прихожей	4, 5, 8	C10	30 мА, тип A	ВВГнг(A)-LS 3×1,5	87	0,6	37
3	освещение и вентиляторы ванной и гостевого санузла	5, 7, 8, 9	C10	30 мА, тип A	ВВГнг(A)-LS 3×1,5	35	0,15	11
4	розетки спальни	1	C16	30 мА, тип A	ВВГнг(A)-LS 3×2,5	40,2	1,5	6
5	розетки кабинета и детской	3, 6	C16	30 мА, тип A	ВВГнг(A)-LS 3×2,5	44,8	1,5	10
6	розетки гостиной, коридора и прихожей	4, 5, 8	C16	30 мА, тип A	ВВГнг(A)-LS 3×2,5	49	2	8
7	розетки фартука и острова кухни, СВЧ	4	C16	30 мА, тип A	ВВГнг(A)-LS 3×2,5	30,7	3	5
8	варочная панель на острове	4	C32	30 мА, тип A	ВВГнг(A)-LS 3×6	12,4	7	1
9	духовой шкаф	4	C16	30 мА, тип A	ВВГнг(A)-LS 3×2,5	17,8	3	1
10	посудомоечная машина	4	C16	30 мА, тип A	ВВГнг(A)-LS 3×2,5	17,4	2	1
11	холодильник	4	C16	30 мА, тип A	ВВГнг(A)-LS 3×2,5	14,4	0,3	1
12	стиральная машина	7	C16	30 мА, тип A	ВВГнг(A)-LS 3×2,5	15,2	2,2	1
13	розетки ванной и гостевого санузла (фен), полотенцесушители П7, П13**	7, 9	C16	30 мА, тип A	ВВГнг(A)-LS 3×2,5	31,2	2,4	4
14	слаботочный щит (роутер, ONT)	8	C10	30 мА, тип A	ВВГнг(A)-LS 3×1,5	3,5	0,1	1
	Итого по сечениям ВВГнг(A)-LS (все группы щита), м: 3×1,5 — 248,6; 3×2,5 — 260,7; 3×6 — 12,4					521,7		

Примечания

1. Схема однолинейная: одна линия — фаза, N и PE группы; аппараты — в отключённом положении (ГОСТ 2.702, ГОСТ 2.755). Номера групп — как у точек на планах (гр.). За отметку 0,000 принят уровень чистого пола; высота щита — по плану розеток.
2. Розеточные и мокрые линии — через УЗО или дифавтомат с током утечки не более 30 мА (ПУЭ 7.1.79); в санузле выполнить ДСУП (ПУЭ 7.1.87–7.1.88).
3. УЗО тип A — для линий с электроникой, стиральной и посудомоечной машиной, LED-драйверами; тип AC — только для чисто активной нагрузки.
4. Кабель — медный, исполнение нг(A)-LS (ГОСТ 31565-2012); скрытая прокладка только горизонтально и вертикально, фактические трассы зафиксировать исполнительной схемой до закрытия отделкой.
5. Номинал автомата — не выше допустимого тока кабеля: 1,5 мм² — до 10 А, 2,5 мм² — до 16 А. Резерв щита — не менее 20 % модулей.
6. Расчёт нагрузок, токов КЗ, селективности и сечений — по проекту ЭОМ организации с допуском СРО; лист задаёт состав, расположение и группы.
7. УЗИП FV1 — после вводного автомата, проводник к шине PE — кратчайший, без петель. Шина PE щита соединяется с ГЗШ проводником ОСУП; к ГЗШ присоединяются трубы водопровода и отопления на вводе в квартиру (ПУЭ 7.1.87). Шины N и PE — раздельные, после разделения PEN не объединяются.
8. До подключения нагрузки — приёмо-сдаточные испытания с протоколом: сопротивление изоляции линий не менее 0,5 МОм, срабатывание УЗО по току и времени, непрерывность защитных проводников PE (ПУЭ, гл. 1.8).

Изм.	Кол.уч	Лист	№ док.	Подп.	Дата
Разраб.		Кырлан А.С.			04.11.26
Пров.					
ГИП					
Н. контр.					
Утв.					

ГД-2026-008-АИ

Квартира с кабинетом

Общая площадь 127,29* м² · * размеры со скана, не замерены (реестр — л. 6–8, К-1)

Дизайн-проект интерьера

Стадия	Лист	Листов
РП	30	131

Однолинейная схема щита


М б/м

Кырлан Александр Сергеевич

Однолинейная схема щита (продолжение)

Щит квартирный ЩК · резервные аппараты · без масштаба

Продолжение однолинейной схемы щита ЩК, начало — лист 30

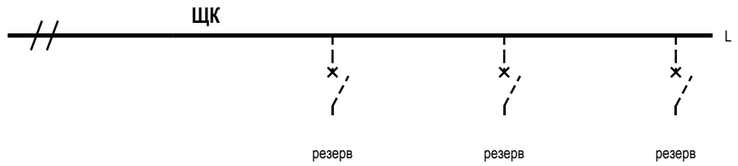

Примечания

1. Лист — продолжение однолинейной схемы щита ЩК: начало, данные щитка и условные обозначения — лист 30. Ввод, учёт, вводной аппарат, УЗИП, шины N и PE и ГЗШ показаны там же; шина L листа — та же шина щита.
2. Схема однолинейная: одна линия — фаза, N и PE группы; аппараты — в отключённом положении (ГОСТ 2.702, ГОСТ 2.755). Номера групп — как у точек на планах (гр.). За отметку 0,000 принят уровень чистого пола; высота щита — по плану розеток.
3. Розеточные и мокрые линии — через УЗО или дифавтомат с током утечки не более 30 мА (ПУЭ 7.1.79); в санузле выполнить ДСУП (ПУЭ 7.1.87–7.1.88).
4. УЗО тип A — для линий с электроникой, стиральной и посудомоечной машиной, LED-драйверами; тип AC — только для чисто активной нагрузки.
5. Кабель — медный, исполнение нг(A)-LS (ГОСТ 31565-2012); скрытая прокладка только горизонтально и вертикально, фактические трассы зафиксировать исполнительной схемой до закрытия отделкой.
6. Номинал автомата — не выше допустимого тока кабеля: 1,5 мм² — до 10 А, 2,5 мм² — до 16 А. Резерв щита — не менее 20 % модулей.
7. Расчёт нагрузок, токов КЗ, селективности и сечений — по проекту ЭОМ организации с допуском СРО; лист задаёт состав, расположение и группы.
8. До подключения нагрузки — приёмо-сдаточные испытания с протоколом: сопротивление изоляции линий не менее 0,5 МОм, срабатывание УЗО по току и времени, непрерывность защитных проводников PE (ПУЭ, гл. 1.8).

Допущения и предложения на листе

Основа листа: размеры сняты с растрового плана заказчика с частичными размерами: рисунок не в масштабе, помещения выровнены по подписанным размерам мебели и проходов; контрольный обмер не выполнен (К-1); высота потолка 2700 мм принята: на плане заказчика её нет (К-2); толщины стен 300 / 120 мм приняты по плану заказчика, не замерены (К-1); разрешённая мощность 15 кВт принята по типовым ТУ для квартиры, ТУ заказчиком не переданы (К-4); подрайон климата не задан — принят не северный (жилые от 2,5 м) (К-6).
См. лист открытых вопросов (лист 6, записи К-1, К-2, К-4, К-6).

Изм.	Кол.уч	Лист	№ док.	Подп.	Дата
Разраб.		Кырлан А.С.			04.11.26
Пров.					
ГИП					
Н. контр.					
Утв.					

ГД-2026-008-АИ

Квартира с кабинетом

Общая площадь 127,29* м² · * размеры со скана, не замерены (реестр — л. 6–8, К-1)

Дизайн-проект интерьера

Стадия	Лист	Листов
РП	31	131

Однолинейная схема щита (продолжение)

М б/м


Кырлан Александр Сергеевич

выпуск 04.11.2026 № 4177cbe7a3 · стр. 34 из 166

План принципиальных трасс

Силовые трассы и объёмы электромонтажа, слаботочка в объёмах · размеры в мм

ПРЕДВАРИТЕЛЬНО · не для производства работ · открыто пунктов: 13 (реестр — л. 6–8)

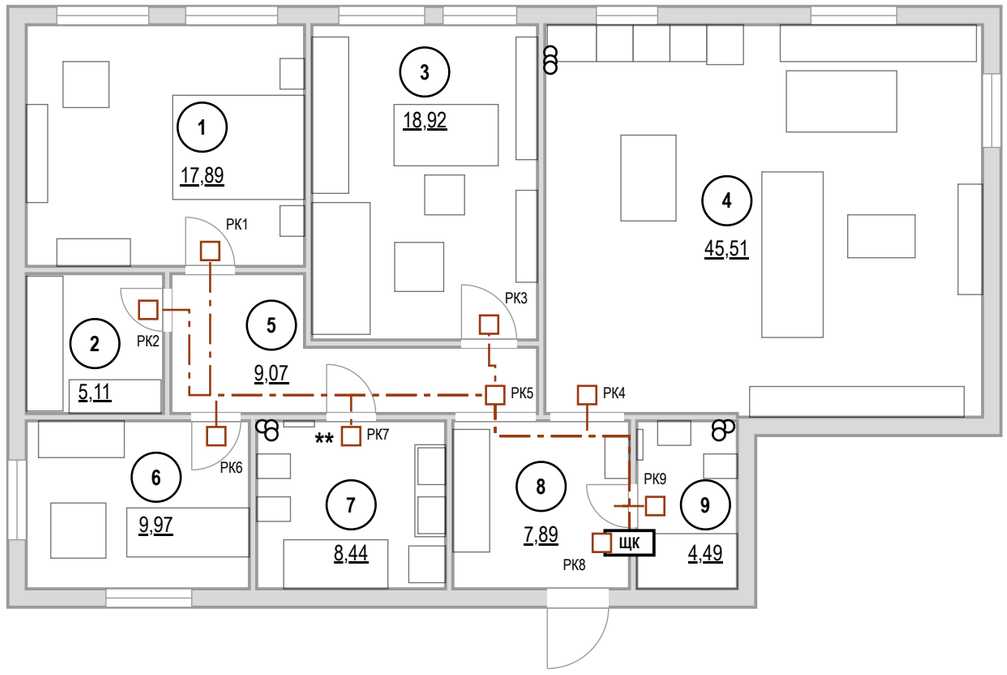

Кабель по группам ВВГнг(А)-LS, м

Гр.	мм²	Трасса	Данные
1	3×1,5	123,1	123,1
2	3×1,5	87,2	87
3	3×1,5	36,8	35
4	3×2,5	40,2	40,2
5	3×2,5	44,8	44,8
6	3×2,5	49,7	49
7	3×2,5	30,9	30,7

Гр.	мм²	Трасса	Данные
8	3×6	12,4	12,4
9	3×2,5	17,8	17,8
10	3×2,5	17,4	17,4
11	3×2,5	14,4	14,4
12	3×2,5	17,6	15,2
13	3×2,5	31	31,2
14	3×1,5	3,5	3,5
Σ		**526,8**	**521,7**

Экспликация помещений

№	Помещение	Площадь, м²
1	Спальня	17,89
2	Гардеробная-постирочная	5,11
3	Кабинет	18,92
4	Кухня-гостиная	45,51
5	Коридор	9,07
6	Детская	9,97
7	Ванная	8,44
8	Прихожая	7,89
9	Санузел гостевой	4,49
	Итого (общая площадь)	127,29

Объёмы прокладки

Работа, материал	Ед.	Кол.
Гофротруба Ø20 в потолочном пространстве	м	218
Кабель-канал плинтуса для силовых линий	м	134,4
Короб или накладной канал для вертикальных спусков и подъёмов	м	87,8
Коробка распределительная (РК) над дверью помещения	шт	9
Слаботочка: кабель домофона	м	5,7
Слаботочка: Кабель коаксиальный RG-6 (75 Ом) к розеткам ТВ	м	57
Слаботочка: U/UTP кат. 6 (LAN, Wi-Fi, камеры)	м	110,6
Слаботочка: гофротруба Ø20 отдельно от силовых	м	156

Штробы — только после заключения

Работа	Ед.	Кол.
Вертикальные штробы 20×20 мм от потолка до каждой настенной точки (в маршрут без штроб не входят)	м	105,42

Условные обозначения

- **ЩК** — щит квартирный
- РК — распределительная коробка над дверью помещения
- магистраль от щита к РК: потолочное пространство, гофра
- мебель и сантехприборы — подложка

Допущения и предложения на листе

Основа листа: размеры сняты с растрового плана заказчика с частичными размерами: рисунок не в масштабе, помещения выровнены по подписанным размерам мебели и проходов; контрольный обмер не выполнен (К-1); высота потолка 2700 мм принята: на плане заказчика её нет (К-2); толщины стен 300 / 120 мм приняты по плану заказчика, не замерены (К-1); разрешённая мощность 15 кВт принята по типовым ТУ для квартиры, ТУ заказчиком не переданы (К-4); подрайон климата не задан — принят не северный (жилые от 2,5 м) (К-6).
Знак «**» — предложение проектировщика, заказчиком не утверждено (согласовать с заказчиком): ЩС — щит слаботочный: место и состав; ИЗ-2, К-5: дверь пом. 7 (стена А) — Проём сдвинут вдоль стены А от угла Б: offset 2300 → 1200 — утверждено автором (ИЗ-2, Кырлан А.С.).
См. лист открытых вопросов (лист 6, записи К-1, К-2, К-4–К-6; лист 7, запись ИЗ-2).

Примечания

1. За отметку 0,000 принят уровень чистого пола. Высоты Н — от чистого пола до оси изделия; привязки — от чистовой грани стены до оси механизма (у рамки на несколько постов — до оси рамки).
2. Розеточные и мокрые линии — через УЗО или дифавтомат с током утечки не более 30 мА (ПУЭ 7.1.79); в санузле выполнить ДСУП (ПУЭ 7.1.87–7.1.88).
3. Кабель — медный, исполнение нг(А)-LS (ГОСТ 31565-2012); скрытая прокладка только горизонтально и вертикально, фактические трассы зафиксировать исполнительной схемой до закрытия отделкой.
4. Расчёт нагрузок, токов КЗ, селективности и сечений — по проекту ЭОМ организации с допуском СРО; лист задаёт состав, расположение и группы.
5. Длины — по плану: от щита вверх в потолочное пространство, по дверям и коридору без захода в мокрые помещения к распределительной коробке над дверью, далее к точкам; вертикали считаются вниз и обратно (у последней точки цепочки — в один конец); запас 10 %. Трассы принципиальные: фактическую зафиксировать исполнительной схемой до закрытия отделкой.
6. Несущие стены не определены: штробы в стенах не выполнять. Маршрут проложен без штроб: горизонтали — за потолком в гофре (218 м) и в кабель-канале плинтуса (134,4 м), вертикали — в коробе или накладном канале (154,6 м кабеля). Точек: за потолком — 60, спуск из потолка — 15, по плинтусу — 16, плинтус и подъём 37.
7. Вариант со штробами — работа после технического заключения: 105,42 м вертикальных штроб от потолка до каждой настенной точки; условие — только после технического заключения: стена не несущая (или вертикальная штроба в несущей согласована конструктором), глубина и ширина 20–25 мм, не в зонах 0–2 ванной. Без заключения и согласования конструктора в смету и в график эта работа не входит.
8. В данных проекта (журнал щита) длины кабеля внесены оценкой (522 м), по трассам из геометрии — 527 м (+1 %): к закупке и в смету принимать длины по трассам, а оценку в данных проекта заменить.
9. Слаботочные сети: кабели и точки считаются по лучам от ЩС** (лист слаботочных сетей): 173 м, портов патч-панели и коммутатора не менее 7; из точек 3 предложения листа слаботочки, не подтверждённые заказчиком. Изделия — в ведомости изделий.

1000 мм · печать 1:1

Изм.	Кол.уч	Лист	№ док.	Подп.	Дата
Разраб.		Кырлан А.С.			04.11.26
Пров.					
ГИП					
Н. контр.					
Утв.					

ГД-2026-008-АИ

Квартира с кабинетом

Общая площадь 127,29* м² · * размеры со скана, не замерены (реестр — л. 6–8, К-1)

Дизайн-проект интерьера

Стадия	Лист	Листов
РП	32	131

План принципиальных трасс

М 1:100


Кырлан Александр Сергеевич

выпуск 04.11.2026 № 4177cbe7a3 · стр. 35 из 166

План слаботочных сетей

Интернет, ТВ, домофон · размеры в мм · высоты от чистого пола

ПРЕДВАРИТЕЛЬНО · не для производства работ · открыто пунктов: 13 (реестр — л. 6–8)

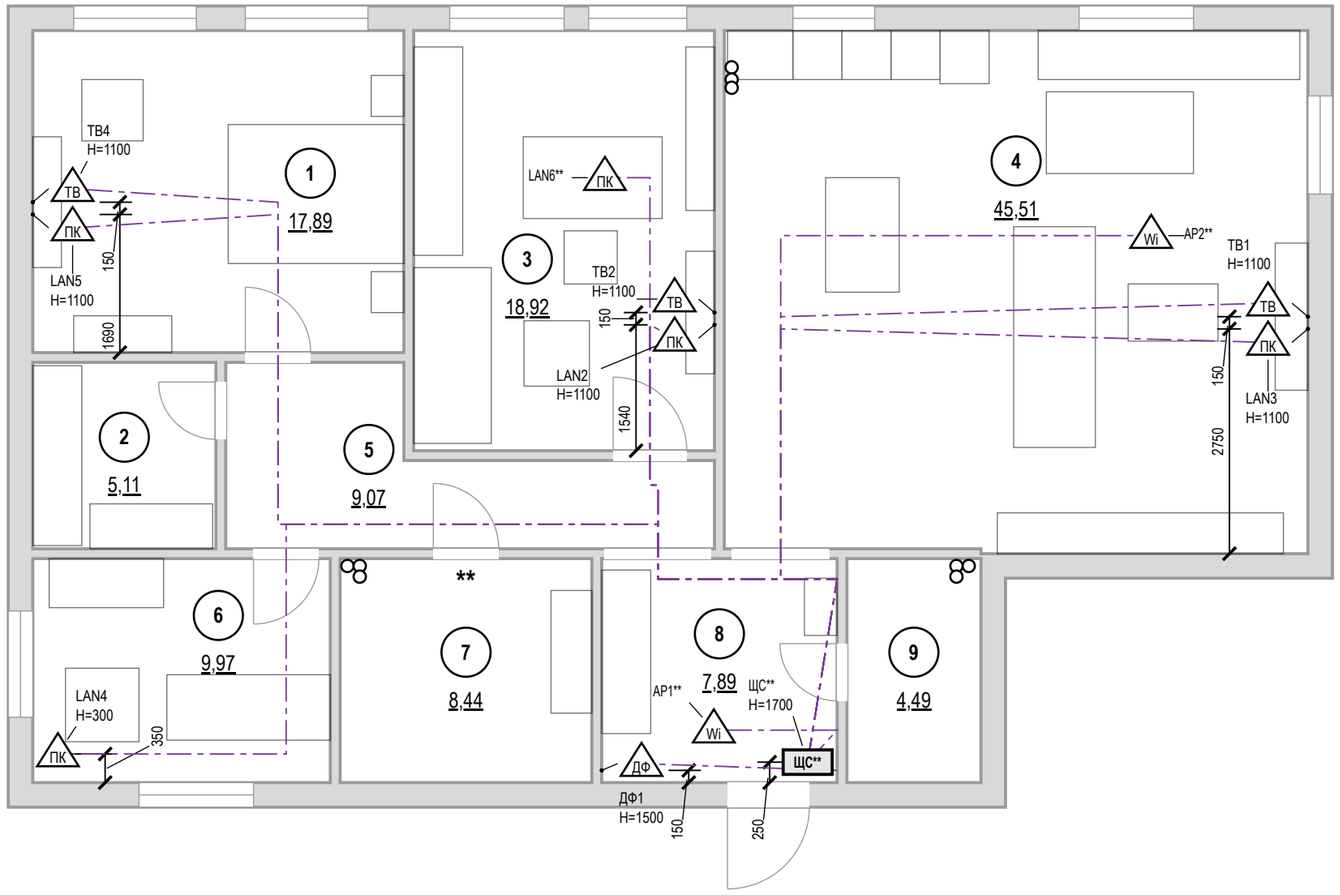

Ведомость слаботочных точек

Марка	Пом.	Назначение	H, мм	Кабель
TB4	1	розетка ТВ	1100	RG-6
LAN5	1	розетка LAN (RJ45)	1100	U/UTP кат. 6
TB2	3	розетка ТВ	1100	RG-6
LAN2	3	розетка LAN (RJ45)	1100	U/UTP кат. 6
LAN6**	3	розетка LAN (RJ45)	0	U/UTP кат. 6
TB1	4	розетка ТВ	1100	RG-6
LAN3	4	розетка LAN (RJ45)	1100	U/UTP кат. 6
AP2**	4	точка доступа Wi-Fi		U/UTP кат. 6
LAN4	6	розетка LAN (RJ45)	300	U/UTP кат. 6
ЩС**	8	щит слаботочный	1700	ввод пров.
ДФ1	8	домофон (трубка)	1500	по системе
AP1**	8	точка доступа Wi-Fi		U/UTP кат. 6

Условные обозначения

- **ЩС** — щит слаботочный: ввод провайдера, роутер, коммутатор
- ПК — розетка компьютерная RJ45
- ТВ — розетка телевизионная
- ДФ — трубка или монитор домофона
- Wi — точка доступа Wi-Fi (питание PoE)
- кабель от ЩС до точки, отдельным лучом
- мебель и сантехприборы — подложка
- стояк: К1 — канализация, В1 — ХВС, Т3 — ГВС
- 1 — номер помещения, площадь м²

Допущения и предложения на листе

Основа листа: размеры сняты с растрового плана заказчика с частичными размерами: рисунок не в масштабе, помещения выровнены по подписанным размерам мебели и проходов; контрольный обмер не выполнен (К-1); высота потолка 2700 мм принята: на плане заказчика её нет (К-2); толщины стен 300 / 120 мм приняты по плану заказчика, не замерены (К-1); разрешённая мощность 15 кВт принята по типовым ТУ для квартиры, ТУ заказчиком не переданы (К-4); подрайон климата не задан — принят не северный (жилые от 2,5 м) (К-6).

Знак «**» — предложение проектировщика, заказчиком не утверждено (согласовать с заказчиком): LAN6 — стол К62 стоит посреди помещения — питание из лючка в полу под столом: трасса в конструкции пола (толщина стяжки — по обмеру) — согласовать с заказчиком; AP2, AP1 — точка доступа Wi-Fi: число и места; ЩС — щит слаботочный: место и состав; ИЗ-2, К-5: дверь пом. 7 (стена А) — Проём сдвинут вдоль стены А от угла Б: offset 2300 → 1200 — утверждено автором (ИЗ-2, Кырлан А.С.).

См. лист открытых вопросов (лист 6, записи К-1, К-2, К-4–К-6; лист 7, запись ИЗ-2).

Примечания

1. За отметку 0,000 принят уровень чистого пола. Высоты H — от чистого пола до оси изделия; привязки — от чистовой грани стены до оси механизма (у рамки на несколько постов — до оси рамки).
2. Высота установки, не указанная на плане: розетки LAN и ТВ — 300 мм от чистого пола.
3. Слаботочные кабели — отдельно от силовых: в своей трубе или лотке, при параллельной прокладке не ближе 100 мм к силовым, пересечения под прямым углом; каждую точку — отдельным кабелем от ЩС** без скруток.
4. Трассы на листе — принципиальные; фактические зафиксировать исполнительной схемой до закрытия отделкой. Силовые линии, УЗО 30 мА, ДСУП, кабель нг(A)-LS — по листам розеток и щита.
5. Проект силовой части и расчёт токов КЗ — по проекту ЭОМ; слаботочная часть согласуется с провайдером и управляющей компанией (домофон, коллективное ТВ).

1000 мм · печать 1:1

Изм.	Кол.уч	Лист	№ док.	Подп.	Дата
Разраб.		Кырлан А.С.			04.11.26
Пров.					
ГИП					
Н. контр.					
Утв.					

ГД-2026-008-АИ

Квартира с кабинетом

Общая площадь 127,29* м² · * размеры со скана, не замерены (реестр — л. 6–8, К-1)

Дизайн-проект интерьера

Стадия	Лист	Листов
РП	33	131

План слаботочных сетей

М 1:75

Кырлан Александр Сергеевич

выпуск 04.11.2026 № 4177cbe7a3 · стр. 36 из 166

04

Отопление и вентиляция

Кырлан Александр Сергеевич

выпуск 04.11.2026 № 417/cbe7a3 · стр. 37 из 166

План вентиляции

Вытяжка, приток, переток · кондиционирование не предусмотрено · размеры в мм · высоты от чистого пола


ПРЕДВАРИТЕЛЬНО · не для производства работ · открыто пунктов: 13 (реестр — л. 6–8)

Допущения и предложения на листе

Основа листа: размеры сняты с растрового плана заказчика с частичными размерами: рисунок не в масштабе, помещения выровнены по подписанным размерам мебели и проходов; контрольный обмер не выполнен (К-1); высота потолка 2700 мм принята: на плане заказчика её нет (К-2); толщины стен 300 / 120 мм приняты по плану заказчика, не замерены (К-1); разрешённая мощность 15 кВт принята по типовым ТУ для квартиры, ТУ заказчиком не переданы (К-4); подрайон климата не задан — принят не северный (жилые от 2,5 м) (К-6).

Знак «**» — предложение проектировщика, заказчиком не утверждено (согласовать с заказчиком): ИЗ-2, К-5: дверь пом. 7 (стена А) — Проём сдвинут вдоль стены А от угла Б: offset 2300 → 1200 — утверждено автором (ИЗ-2, Кырлан А.С.); ИЗ-8: Кх6 — Остров сдвинут от кухонного ряда: торец острова стоял в 900 мм от фронта ПММ Кх3 и модуля Кх4 — меньше 1000 мм (СП 31-107-2004, п. 6.1.12) и меньше 1200 мм, при которых открытые ПММ и ящики не перекрывают проход.

См. лист открытых вопросов (лист 6, записи К-1, К-2, К-4–К-6; лист 7, запись ИЗ-2; лист 8, запись ИЗ-8).

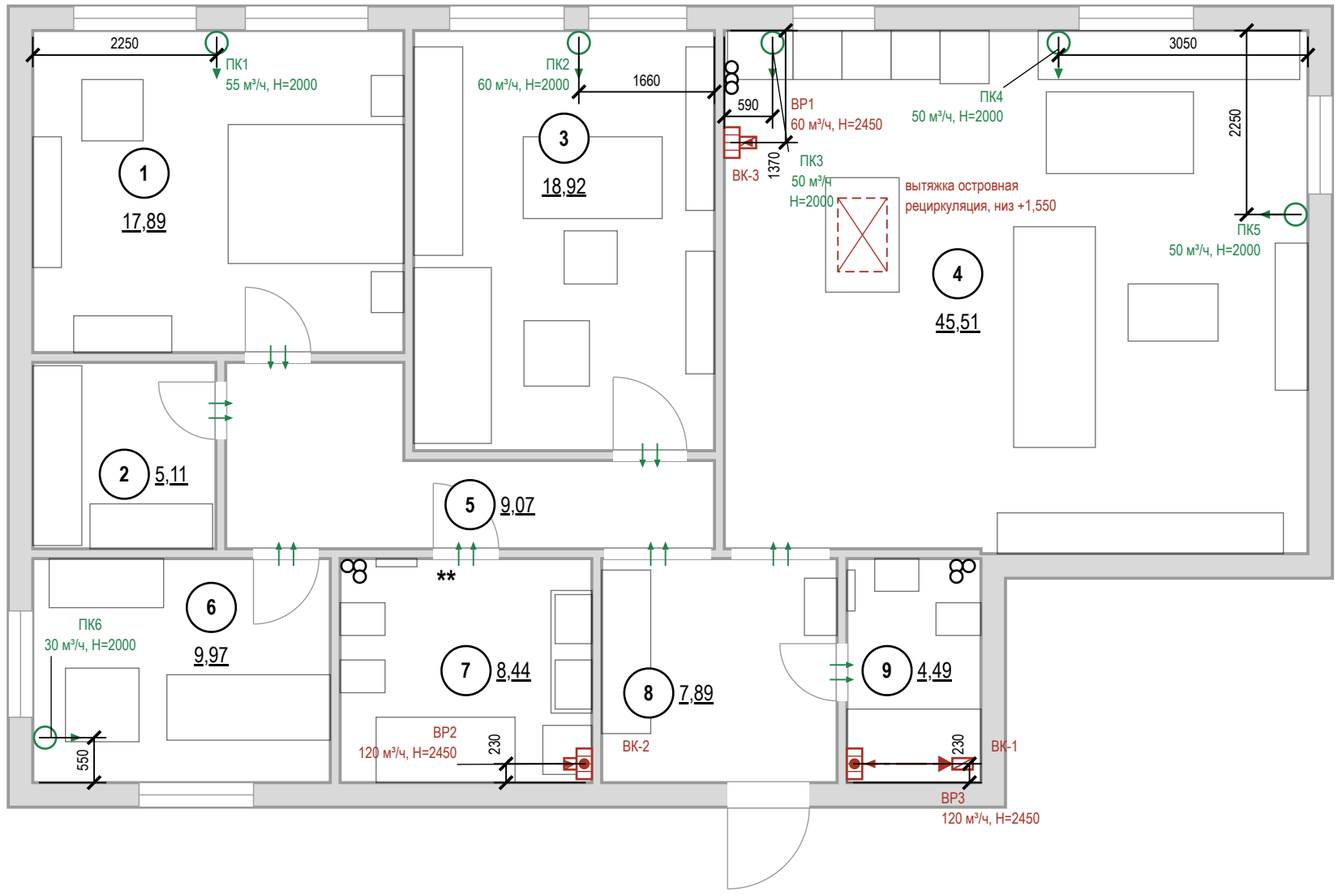

Условные обозначения

- стояк: К1 — канализация, В1 — ХВС, Т3 — ГВС
- номер помещения, площадь м²
- вытяжная решётка в вентканал: марка, расход м³/ч, Н центра от чистого пола
- вытяжная решётка с бытовым вентилятором и обратным клапаном: марка, расход, Н
- приточный клапан (КИВ) в наружной стене: марка, расход, Н центра
- переток: зазор под полотном или переточная решётка
- кухонная вытяжка над варочной панелью
- вентканал ВК-N в стене или вентблоке
- воздуховод в коробе под потолком (за подшивным потолком) до вентканала
- отдельный вход воздуховода в вентканал, обратный клапан
- ** «**» — предложение проектировщика, заказчиком не утверждено

Воздухообмен, м³/ч

№	Помещение	Выт. норма	Выт. проект	Прит. норма	Прит. проект	Устрой-ства
1	Спальня			54	55	ПК1
2	Гардеробная-постирочная	3				переток
3	Кабинет			57	60	ПК2
4	Кухня-гостиная	60	60	137	150	ВР1, ПК3, ПК4, ПК5
6	Детская			30	30	ПК6
7	Ванная	50	120			ВР2
9	Санузел гостевой	50	120			ВР3
	Итого	**163**	**300**	**278**	**295**	
	Норма по жильцам: 30×3			90		

Воздухообмен квартиры — по большей из сумм притока и вытяжки: норма 278 м³/ч, проект 300 м³/ч.

Вытяжка не меньше притока — баланс сведён.

Примечания

1. Расчёт систем ОВ и подбор оборудования — проектная организация с допуском СРО; лист даёт места, трассы и привязки.
2. Нормы вытяжки — СП 54.13330.2022 (Изм. 1, 2), табл. 7.1: кухня с электроплитой 60 м³/ч, с газовой 100; ванная и совмещённый санузел 50; уборная 25; гардеробная 0,2 ч⁻¹. Приток в жилые — 3 м³/ч на 1 м² (менее 20 м² общей площади на человека), иначе 30 м³/ч на человека.
3. Вентканалы и шахты не сужать, не переносить и не закрывать; вентилятор и кухонная вытяжка — через обратный клапан, без перекрытия естественной тяги; ВР3 — воздуховодом до ВК-1 ≈ 1,3 м в коробе под потолком.
4. Проектные расходы — не ниже нормы, вытяжка сведена с притоком вентиляторами мокрых помещений. Клапаны — в простенке у окна, центр 2000 мм, не над кроватью, не ближе 300 мм к стоякам отопления; типоразмер — на расход.
5. Кухня-гостиная (пом. 4): вытяжка островная потолочная над Кх6** 600×900, низ +1,550 — рециркуляционная (угольный фильтр): воздуховода и входа в канал нет, в воздухообмен не включена; вытяжка кухни — через вентканал. Крепление к плите перекрытия — закладная по паспорту модели (план потолков), вывод питания на потолке — план электрики (ИЗ-8).
6. Переток — зазор под полотнами межкомнатных дверей или переточная решётка.
7. Кондиционирование заданием не предусмотрено; при установке трассы фреона и дренажа (не менее 40 мм/м, в К1 через сифон) и питание заложить до черновых работ.
8. Привязки оборудования — по паспортам приобретённых моделей, до черновых работ.

1000 мм · печать 1:1

Изм.	Кол.уч	Лист	№ док.	Подп.	Дата
Разраб.		Кырлан А.С.			04.11.26
Пров.					
ГИП					
Н. контр.					
Утв.					

ГД-2026-008-АИ

Квартира с кабинетом

Общая площадь 127,29* м² · * размеры со скана, не замерены (реестр — л. 6–8, К-1)

Дизайн-проект интерьера

Стадия	Лист	Листов
РП	34	131

План вентиляции


М 1:75

Кырлан Александр Сергеевич

выпуск 04.11.2026 № 4177cbe7a3 · стр. 38 из 166

План отопления

Радиаторы, стояки, подводки · размеры в мм · высоты от чистого пола

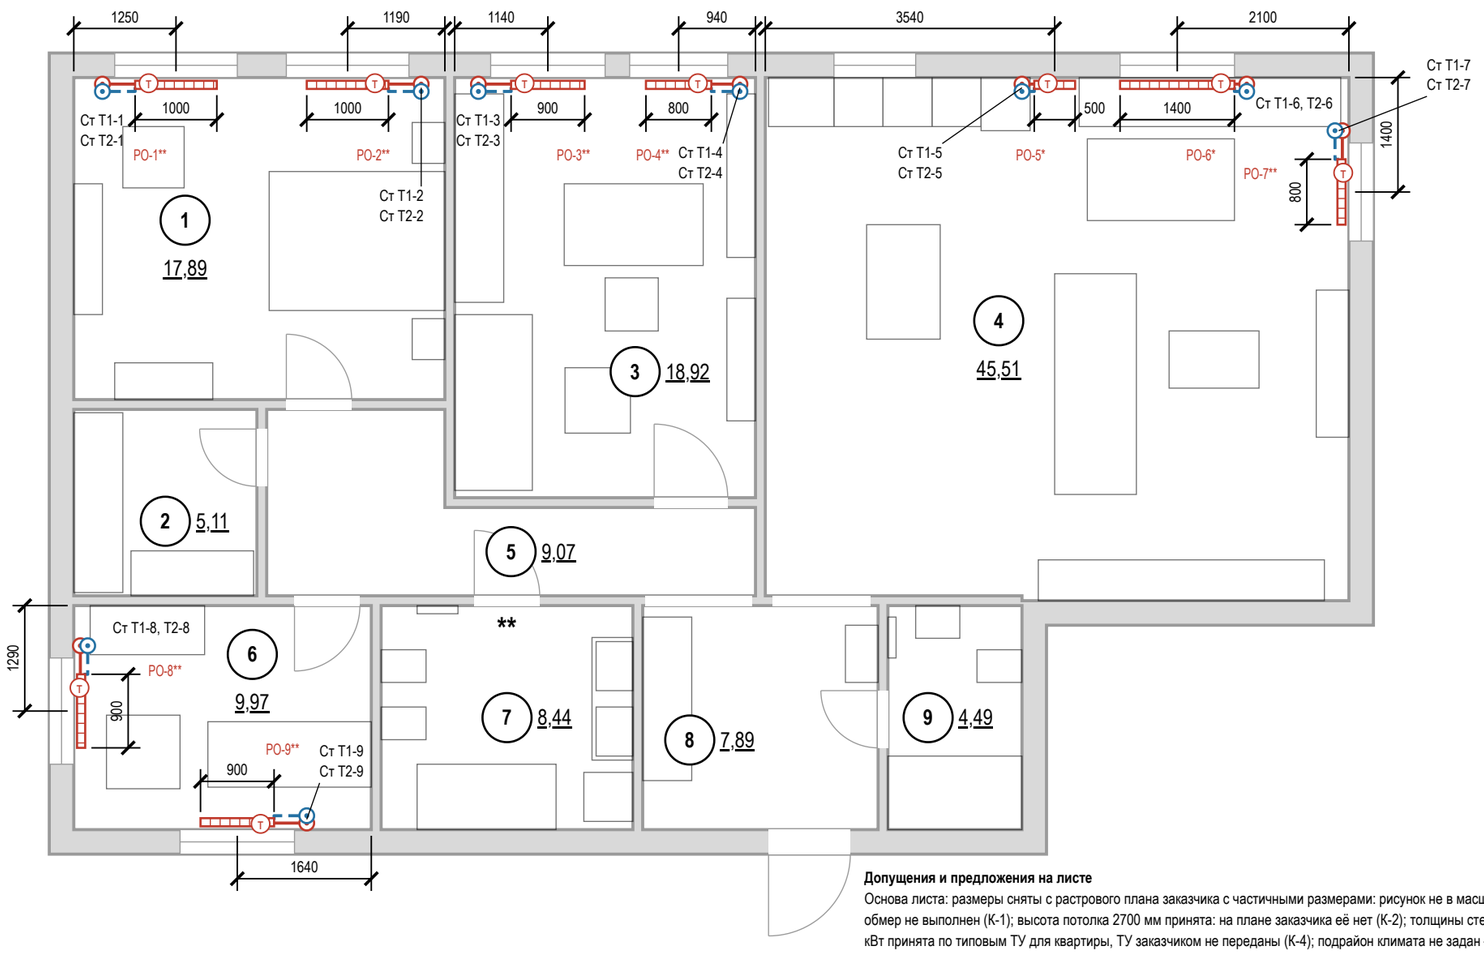

Условные обозначения

- (1) — номер помещения, площадь м²
- радиатор отопления (марка РО-N, длина по плану)
- клапан с термоголовкой на подаче
- стояк отопления, подающий (Ст Т1-N)
- стояк отопления, обратный (Ст Т2-N)
- Т1 — отопление, подающий трубопровод
- Т2 — отопление, обратный трубопровод
- ** — «**» — предложение проектировщика, заказчиком не утверждено

Ведомость радиаторов

Марка	Помещение	Тип	Д×В×Г, мм	Низ / стена	Q, Вт
РО-1**	1. Спальня		1000×500×100	120 / 40	расч.
РО-2**	1. Спальня		1000×500×100	120 / 40	расч.
РО-3**	3. Кабинет		900×500×100	120 / 40	расч.
РО-4**	3. Кабинет		800×500×100	120 / 40	расч.
РО-5*	4. Кухня-гостиная		500×600×100	120 / 40	расч.
РО-6*	4. Кухня-гостиная	тенельный 22, высота 200 (низом)	1400×200×100	120 / 40	расч.
РО-7**	4. Кухня-гостиная		800×500×100	120 / 40	расч.
РО-8**	6. Детская		900×500×100	120 / 40	расч.
РО-9**	6. Детская		900×500×100	120 / 40	расч.

Низ — от чистого пола, стена — зазор до задней панели, мм.

Привязки — до обмера

Стояки отопления в исходных данных не заданы: показаны у откосов окон и у торцов приборов, подводки принципиально. До черновых работ — обмер стояков и паспорта приборов; лист перевыпустить по факту.

Допущения и предложения на листе

Основа листа: размеры сняты с растрового плана заказчика с частичными размерами: рисунок не в масштабе, помещения выровнены по подписанным размерам мебели и проходов; контрольный обмер не выполнен (К-1); высота потолка 2700 мм принята: на плане заказчика её нет (К-2); толщины стен 300 / 120 мм приняты по плану заказчика, не замерены (К-1); разрешённая мощность 15 кВт принята по типовым ТУ для квартиры, ТУ заказчиком не переданы (К-4); подрайон климата не задан — принят не северный (жилые от 2,5 м) (К-6).

Знак «*» — принято, не замерено и не подтверждено (замерить на объекте): ИЗ-6, К-1, К-19: РО-5 — перенос с оси окна 1 (offset 1050, 700 мм — был внутри модулей Кх3 ПММ и Кх4 с ящиками, Кф-1) на свободный участок наружной стены А между колонной Кх1 и банкеткой Кх7 (х 11750…12250, по 50 мм до корпусов): прибор открыт, гарнитур под окном без коллизии — решение исполнителя (ОВ) утверждено автором (ИЗ-6); ширина 500 вместо 700 — мощность сверить теплотехническим расчётом ОВ (при нехватке — вертикальный прибор на том же месте); стояки и подводки не замерены (К-1); ИЗ-7, К-1, К-19: РО-6 — низкий панельный прибор под сиденьем банкетки-экрана Кх7 у окна 2: было 900×600 (верх +720) — под сиденье банкетки не вставал (Кф-2); стало 1400×200, низ +120, верх +320 — по ширине окна, длина компенсирует малую высоту; мощность сверить теплотехническим расчётом ОВ (при нехватке — внутрипольный конвектор у окна).

Знак «**» — предложение проектировщика, заказчиком не утверждено (согласовать с заказчиком): ИЗ-2, К-5: дверь пом. 7 (стена А) — Проём сдвинут вдоль стены А от угла Б: offset 2300 → 1200 — утверждено автором (ИЗ-2, Кырлан А.С.); К-1: РО-1, РО-2, РО-3, РО-4, РО-7, РО-8, РО-9 — прибор под окном по оси проёма, ширина ≈ 0,7 ширины окна — предложение ОВ (лист ОВ выводил его сам до, теперь он в данных — один источник для листа, мебели, DXF и IFC); стояки и подводки отопления не замерены, мощность — по теплотехническому расчёту ОВ.

Открытые вопросы и конфликты по листу: К-19.

См. лист открытых вопросов (лист 6, записи К-1, К-2, К-4–К-6; лист 7, записи ИЗ-2, К-19; лист 8, записи ИЗ-6, ИЗ-7).

Примечания

1. Расчёт системы отопления, теплопотерь и подбор приборов — проектная организация с допуском СРО; лист даёт места и привязки.
2. Тип, длина и мощность радиаторов — по теплотехническому расчёту; лист задаёт места, зазоры и подключение.
3. Зазоры радиатора: низ не менее 100 мм от чистого пола, верх не менее 100 мм до подоконника, 30–50 мм от стены до задней панели; центр по оси окна с допуском ±20 мм. Верх до подоконника — 180 мм (РО-6* — 580).
4. Радиаторы не закрывать глухими коробами и мебелью; перенос и замена приборов в многоквартирном доме — переустройство, согласование с управляющей организацией (ЖК РФ ст. 25–26); вынос на лоджию запрещён.
5. Исключение — экран-мебель с решёткой: Кх7 (пом. 4), щель 60 мм у стены, решётка в лицевой панели, зазор до прибора 50 мм: теплоотдача прибора за экраном снижается — мощность с учётом экрана по теплотехническому расчёту; сиденье над прибором — съёмное для доступа к крану.
6. Трубы отопления через межквартирные стены не прокладывать (СП 51.13330.2011, п. 9.19); через перекрытия и перегородки — в гильзах.
7. Привязки приборов и подводок — по паспортам приобретённых радиаторов и клапанов, до черновых работ.
8. До закрытия отделкой трубопроводы отопления испытать гидростатическим давлением с оформлением акта (СП 73.13330.2016, 7.2–7.3).

1000 мм · печать 1:1

Изм.	Кол.уч	Лист	№ док.	Подп.	Дата

Разраб.	Кырлан А.С.		04.11.26
Пров.			
ГИП			
Н. контр.			
Утв.			

ГД-2026-008-АИ

Квартира с кабинетом

Общая площадь 127,29* м² · * размеры со скана, не замерены (реестр — л. 6–8, К-1)

Дизайн-проект интерьера

Стадия	Лист	Листов
РП	35	131

План отопления

М 1:75

Кырлан Александр Сергеевич

выпуск 04.11.2026 № 4177cbe7a3 · стр. 39 из 166

05

Водоснабжение и канализация

Кырлан Александр Сергеевич


выпуск 04.11.2026 № 4177cbe7a3 · стр. 40 из 166

План выводов сантехники


Выводы В1, Т3, К1 · привязки от чистовых стен · высоты от чистого пола, мм

ПРЕДВАРИТЕЛЬНО · не для производства работ · открыто пунктов: 13 (реестр — л. 6–8)

Фрагмент 1. Ванная (пом. 7)

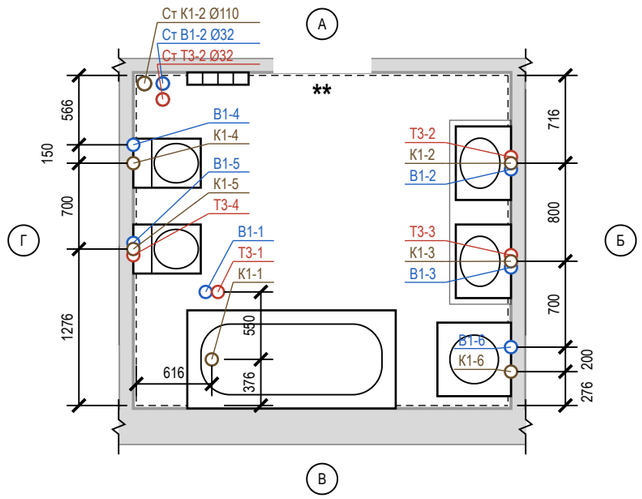


Фрагмент 2. Санузел гостевой (пом. 9)

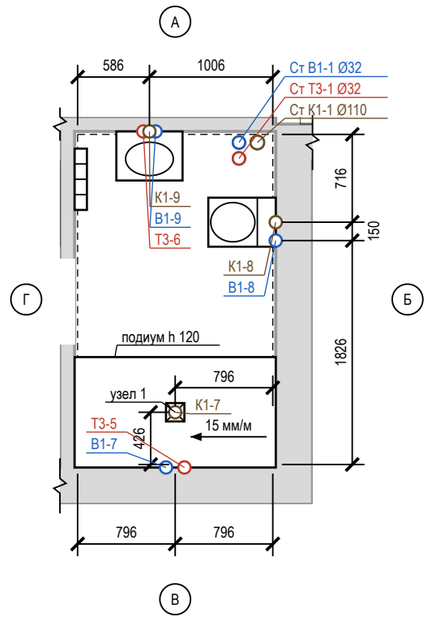

Допущения и предложения на листе. Знак «**» предложено (согласовать). См. лист открытых вопросов (листы 6–8).

Фрагмент 3. Кухня-гостиная (пом. 4)

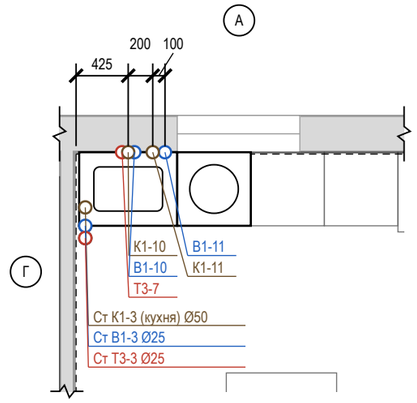

Условные обозначения

- вывод В1 (код — в ведомости привязок)
- вывод Т3 (код — в ведомости привязок)
- вывод К1 (код — в ведомости привязок)
- сантехприбор по расстановке (габарит модели)
- чистовая поверхность стены (от неё привязки)
- стояк «Ст К1-N / Ст В1-N» (ГОСТ 21.601), Ø мм
- линия обрыва (граница фрагмента)
- трап / лоток в полу
- направление уклона К1 / пола: Ø, мм на 1 м
- обозначение стены А–Г (как на развёртках)

Ведомость привязок выводов

Код	Прибор	Ø	Н, мм	Привязка от чист. стен, мм	Прим.
В1-1	П1** ванна	½"	0	566 от Г; 926 от В	в полу под стойку смесителя
Т3-1	П1** ванна	½"	0	666 от Г; 926 от В	в полу под стойку смесителя
К1-1	П1** ванна	Ø50	0	616 от Г; 376 от В	выпуск ванны в пол
В1-2	П2 умывальник	½"	550	ст. Б: 766 от А	межос. 100
Т3-2	П2 умывальник	½"	550	ст. Б: 666 от А	межос. 100
К1-2	П2 умывальник	Ø50	500	ст. Б: 716 от А	
В1-3	П3 умывальник	½"	550	ст. Б: 1126 от В	межос. 100
Т3-3	П3 умывальник	½"	550	ст. Б: 1226 от В	межос. 100
К1-3	П3 умывальник	Ø50	500	ст. Б: 1176 от В	
В1-4	П4 унитаз подвесной	½"	1000	ст. Г: 566 от А	в раме инсталляции
К1-4	П4 унитаз подвесной	Ø110	220	ст. Г: 716 от А	
В1-5	П5 биде подвесное	½"	200	ст. Г: 1326 от В	межос. 100, в раме
Т3-4	П5 биде подвесное	½"	200	ст. Г: 1226 от В	межос. 100, в раме
К1-5	П5 биде подвесное	Ø50	200	ст. Г: 1276 от В	
В1-6	П6 стиральная машина	½"	800	ст. Б: 476 от В	кран машины
К1-6	П6 стиральная машина	Ø50	600	ст. Б: 276 от В	
В1-7	П10** душ	½"	1220	ст. В: 721 от Г	межос. 150; 1100 от пола душа (подиум 120, +0,105)
Т3-5	П10** душ	½"	1220	ст. В: 721 от Б	межос. 150; 1100 от пола душа (подиум 120, +0,105)
К1-7	П10** душ	Ø50	120	796 от Б; 426 от В	трап в подиуме 120
В1-8	П11 унитаз подвесной	½"	1000	ст. Б: 866 от А	в раме инсталляции
К1-8	П11 унитаз подвесной	Ø110	220	ст. Б: 716 от А	
В1-9	П12 умывальник	½"	550	ст. А: 636 от Г	межос. 100
Т3-6	П12 умывальник	½"	550	ст. А: 536 от Г	межос. 100
К1-9	П12 умывальник	Ø50	500	ст. А: 586 от Г	
В1-10	Кх2 мойка кухонная	½"	600*	ст. А: 475 от Г	межос. 100
Т3-7	Кх2 мойка кухонная	½"	600*	ст. А: 375 от Г	межос. 100
К1-10	Кх2 мойка кухонная	Ø50	400*	ст. А: 425 от Г	
В1-11	Кх3 посудомоечная машина	½"	550*	ст. А: 725 от Г	кран ПММ в шкафу мойки
К1-11	Кх3 посудомоечная машина	Ø40	550*	ст. А: 625 от Г	слив ПММ в шкафу мойки

* — высота по практике монтажа; сверить по паспорту прибора

Примечания

1. Привязки выводов даны от чистовых поверхностей стен (облицовка на сторону: ванная — 24 мм (штукатурка 10 + клей 5 + плитка 9); санузел гостевой 24 мм (штукатурка 10 + клей 5 + плитка 9); кухня-гостиная — 24 мм (фартук: штукатурка 10 + клей 5 + плитка 9)); эти же грани — на развёртках и в раскладке плитки. Высоты — от чистого пола помещения.
2. Высоты и межосевые, отмеченные «*», приняты по практике монтажа; до черновой разводки сверить по паспорту выбранного прибора (смеситель, инсталляция, сифон).
3. Горячая вода (Т3) — слева от холодной (В1), если смотреть на прибор. Допуск установки выводов: ±5 мм в группе, ±20 мм у отдельно стоящих.
4. Расчёт систем водоснабжения и канализации и подбор оборудования выполняет проектная организация; лист задаёт места и высоты выводов.
5. П1** ванна (В1-1, Т3-1, К1-1) — выводы в полу: пирог пола 35 мм их не укрывает (нужно 185 мм, расчёт — профиль К1 схемы разводки); до решения К-11, К-11 (подъём пола или другой смеситель / выпуск) не выполнять.
6. П10** душ (В1-7, Т3-5, К1-7): трап в подиуме 120 мм — верх подиума у решётки трапа +0,105, к краю поднимается уклоном 15 мм/м: ступень по открытому краю 127 мм (край показан на плане); «узел 1» — на схеме разводки; подиум — предложение, согласовать с заказчиком. Водорозетки В1-7, Т3-5 — 1100 мм от пола душа, то есть 1220 мм от чистого пола помещения: стену размечают до подиума.
7. Посудомоечная машина Кх3: кран и слив — отдельными выводами в шкафу мойки (не за машиной), до машины ≤ 1500 мм.
8. Прибор Кх2 мойка кухонная, Кх3 посудомоечная машина взят из расстановки мебели (по шкафу с мойкой).
9. Стояки в коробах/шахтах не замоноличивать; стояк К1 в коробе — звукоизоляция стояка в коробе без жёсткого контакта с трубой; к арматуре и ревизиям — люк не меньше 300×400.

1000 мм · печать 1:1

Изм.	Кол.уч	Лист	№ док.	Подп.	Дата
Разраб.		Кырлан А.С.			04.11.26
Пров.					
ГИП					
Н. контр.					
Утв.					

ГД-2026-008-АИ

Квартира с кабинетом

Общая площадь 127,29* м² · * размеры со скана, не замерены (реестр — л. 6–8, К-1)

Дизайн-проект интерьера	Стадия	Лист	Листов
	РП	36	131

План выводов сантехники

М 1:50

Кырлан Александр Сергеевич


выпуск 04.11.2026 № 4177cbe7a3 · стр. 41 из 166

Схема разводки водопровода и канализации


Схемы систем В1, Т3, К1 · трассы принципиальные · уклоны в мм на 1 м · план М 1:400, фрагменты М 1:40

ПРЕДВАРИТЕЛЬНО · не для производства работ · открыто пунктов: 13 (реестр — л. 6–8)

План квартиры (М 1:400)

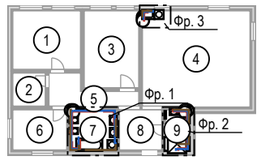

Узел ввода В1, Т3 (по данным, без масштаба)

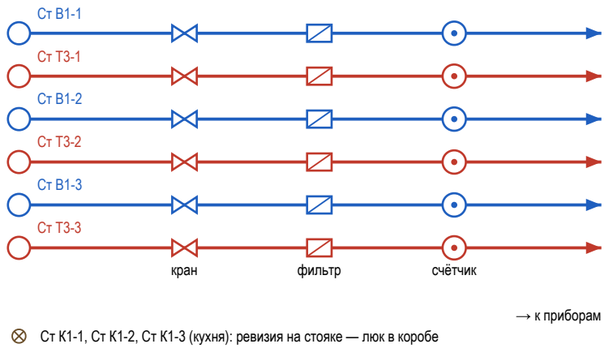


⊗ Ст К1-1, Ст К1-2, Ст К1-3 (кухня): ревизия на стояке — люк в коробе

Условные обозначения


- В1 — водопровод хозяйственно-питьевой (ХВС), PP-R Ø20
- Т3 — горячее водоснабжение, подача (ГВС), PP-R Ø20
- К1 — канализация бытовая
- направление уклона К1 / пола: Ø, мм на 1 м
- ⊗ ревизия (прочистка) К1 — доступ сохранить
- • тройник (ответвление к прибору)
- короб К1 над чистым полом (ГКЛВ под плитку)
- ○ вывод В1 (код — в ведомости привязок)
- ○ вывод Т3 (код — в ведомости привязок)
- ○ вывод К1 (код — в ведомости привязок)
- сантехприбор по расстановке (габарит модели)
- ○ стояк «Ст К1-N / Ст В1-N» (ГОСТ 21.601), Ø мм
- линия обрыва (граница фрагмента)
- граница фрагмента на плане (Фр. N)

Допущения и предложения на листе. Основа листа: размеры сняты с растрового плана заказчика с частичными размерами: рисунок не в масштабе, помещения выровнены по подписанным размерам мебели и проходов; контрольный обмер не выполнен (К-1); высота потолка 2700 мм принята: на плане заказчика её нет (К-2); толщины стен 300 / 120 мм приняты по плану заказчика, не замерены (К-1); разрешённая мощность 15 кВт принята по типовым ТУ для квартиры, ТУ заказчиком не переданы (К-4); подрайон климата не задан — принят не северный (жилые от 2,5 м) (К-6). Знак «**» — предложено, не утверждено (согласовать): ИЗ-2, К-5: дверь пом. 7 (стена А); К-10: П10; К-11: П1. См. лист открытых вопросов (лист 6, записи К-1, К-2, К-4–К-6, К-10, К-11; лист 7, записи ИЗ-2, К-17).


Фр. 1. Ванная (М 1:40)

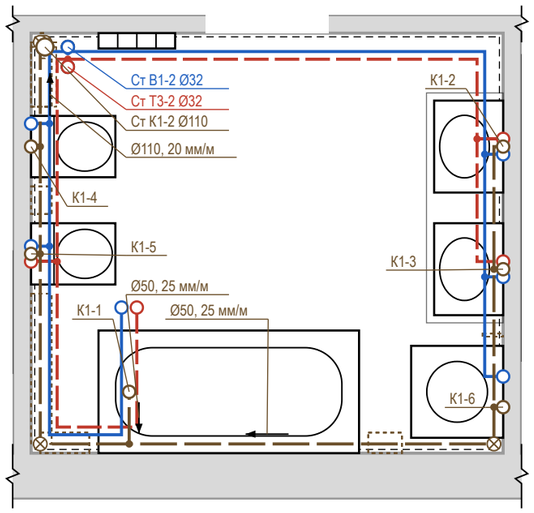

Фр. 2. Санузел гостевой (М 1:40)

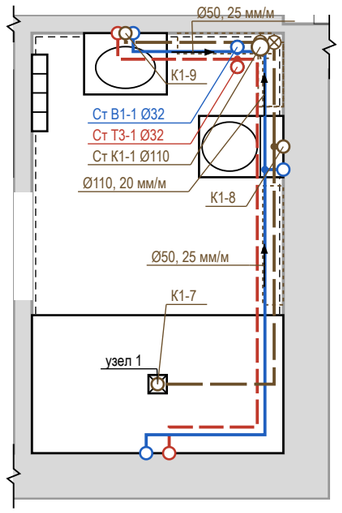

Фр. 3. Кухня-гостиная (М 1:40)

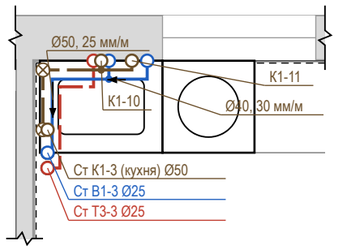


Профиль выпусков К1 (до врезки в стояк)

Выпуск	Прибор	Ø	L, м	i, мм/м	Δh, мм	Прокладка, мм
К1-8	П11 унитаз подвесной	Ø110	0,86	20	17	короб 160×140
К1-4	П4 унитаз подвесной	Ø110	0,80	20	16	короб 160×140
К1-2	П2 умывальник	Ø50	7,64	25	191	короб 280×110
К1-3	П3 умывальник	Ø50	6,84	25	171	короб 260×110
К1-6	П6 стиральная машина	Ø50	5,94	25	149	короб 230×110
К1-1	П1** ванна	Ø50	3,60	25	90	в полу не помещается: 185 > 35; К-11
К1-7	П10** душ	Ø50	3,11	25	78	трап в подиуме 120 (35 + 120 + 14 ≥ 168), далее короб 160×110
К1-5	П5 биде подвесное	Ø50	1,50	25	38	короб 120×110
К1-9	П12 умывальник	Ø50	0,97	25	24	короб 110×110
К1-10	Кх2 мойка кухонная	Ø50	0,86	25	22	над полом за приборами
К1-11	Кх3 посудомоечная машина	Ø40	1,06	30	32	над полом за приборами

Короб h×b: h — от чистого пола, b — от чистовой стены. Стяжка 35 мм — лист полов.

Узел 1. Душ без поддона, трап (П10**)

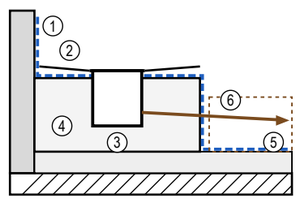

1. гидроизоляция 2 сл. на всю высоту стен душа, по всему санузлу; лента у фланца трапа и в углах
2. плитка, уклон 15 мм/м к трапу (СП 30.13330.2020, п. 17.9)
3. трап с фланцем под гидроизоляцию: монтажная высота 90 мм (до решётки) (принята, по паспорту модели)
4. подиум 120 мм у трапа, ступень 127 мм (ЦПС по гидроизоляции плиты) — предложение, согласовать с заказчиком (К-10)
5. стяжка 35 мм
6. К1 Ø50, i = 25 мм/м, L = 3,11 м, Δh = 78 мм → Ст К1-1; за подиумом — короб 160×110

Пирог ≥ 168 мм = трап 90 + Δh 78 ≤ 35 + подиум 120 + плитка 14 мм

Примечания

1. Трассы принципиальные, построены от стояков вдоль стен помещений; фактическое положение фиксируется исполнительной схемой с привязками (фото с рулеткой) до закрытия.
2. Уклон К1 не менее 1/d и не более 150 мм/м (СП 30.13330.2020, п. 19.1), приняты практические уклоны; поворот — двумя отводами 45°, ревизия после поворота, доступ сохранить. Стояк К1 в коробе — звукоизоляция стояка в коробе, без жёсткого контакта короба с трубой.
3. Решение по К1: стяжка 35 мм не укрывает трубы (нужно Ø + Δh + 45 мм) — выпуски идут над чистым полом вдоль стен: К1-10, К1-11 — за приборами и в раме инсталляции; К1-8, К1-4, К1-2, К1-3, К1-6, К1-5, К1-9 — в коробе ГКЛВ под плитку (размеры в профиле). Короба — на развёртках; отметку низа врезки в стояк замерить до черновых работ.
4. К1-7 (П10** душ, трап): монтажная высота трапа 90 до верха решётки (по паспорту) + уклон 78 = 168 мм ≤ стяжка 35 + подиум 120 + облицовка 14 мм трап в подиуме душевой зоны (узел 1 на этом листе), за краем подиума отвод — в коробе ГКЛВ 160×110 вдоль стены; подиум — предложение (К-10).
5. К1-1 (П1** ванна, выпуск в пол): Δh 90 + Ø50 + 45 = 185 мм > пирога 35 мм — в стяжке не помещается, в короб не уходит: подиум или подъём пола на 150 мм или прибор ближе к стояку — решение К-11, К-11; до решения не выполнять.
6. Отводы К1-2 (7,6 м), К1-3 (6,8 м), К1-6 (5,9 м) длиннее 4 м без вентиляции — у прибора воздушный клапан Ø50 в доступном месте (за люком или в тумбе) либо вентилируемый отвод (EN 12056-2, табл. 4); предложение проектировщика, подбор — проектная организация.
7. Узел ввода В1, Т3 — по данным проекта: кран → фильтр → счётчик. Доступ к арматуре — через люк не меньше 300×400. Водопровод — в штробе стен или в коробах; трубы испытать давлением до закрытия (акт скрытых работ).
8. Расчёт систем, диаметры магистралей и подбор оборудования выполняет проектная организация; врезка и перенос стояков — по согласованию с управляющей организацией. Арматуру и привязки сверить по паспортам приборов.

Изм.	Кол.уч	Лист	№ док.	Подп.	Дата
Разраб.		Кырлан А.С.			04.11.26
Пров.					
ГИП					
Н. контр.					
Утв.					

ГД-2026-008-АИ

Квартира с кабинетом

Общая площадь 127,29* м² · * размеры со скана, не замерены (реестр — л. 6–8, К-1)

Дизайн-проект интерьера

Стадия	Лист	Листов
РП	37	131

Схема разводки водопровода и канализации

М 1:400; 1:40

Кырлан Александр Сергеевич

выпуск 04.11.2026 № 4177cbe7a3 · стр. 42 из 166

Аксонометрическая схема В1 (холодное водоснабжение)


аксонометрия · диаметры, уклоны, отметки, стояки и приборы · трассы принципиальные

Схема В1 (М 1:50; по вертикали и горизонтали один масштаб, глубина — ×0,5 под 45°)

ПРЕДВАРИТЕЛЬНО · не для производства работ · открыто пунктов: 13 (реестр — л. 6–8)

Условные обозначения

- В1 — водопровод хозяйственно-питьевой (ХВС), PP-R Ø20
- вывод В1 (код — в ведомости привязок)
- стояк «Ст К1-N / Ст В1-N» (ГОСТ 21.601), Ø мм
- стояк в плане (на отметке пола); вертикаль — стояк по высоте, разрыв — перекрытие
- тройник (ответвление к прибору)
- кран шаровой

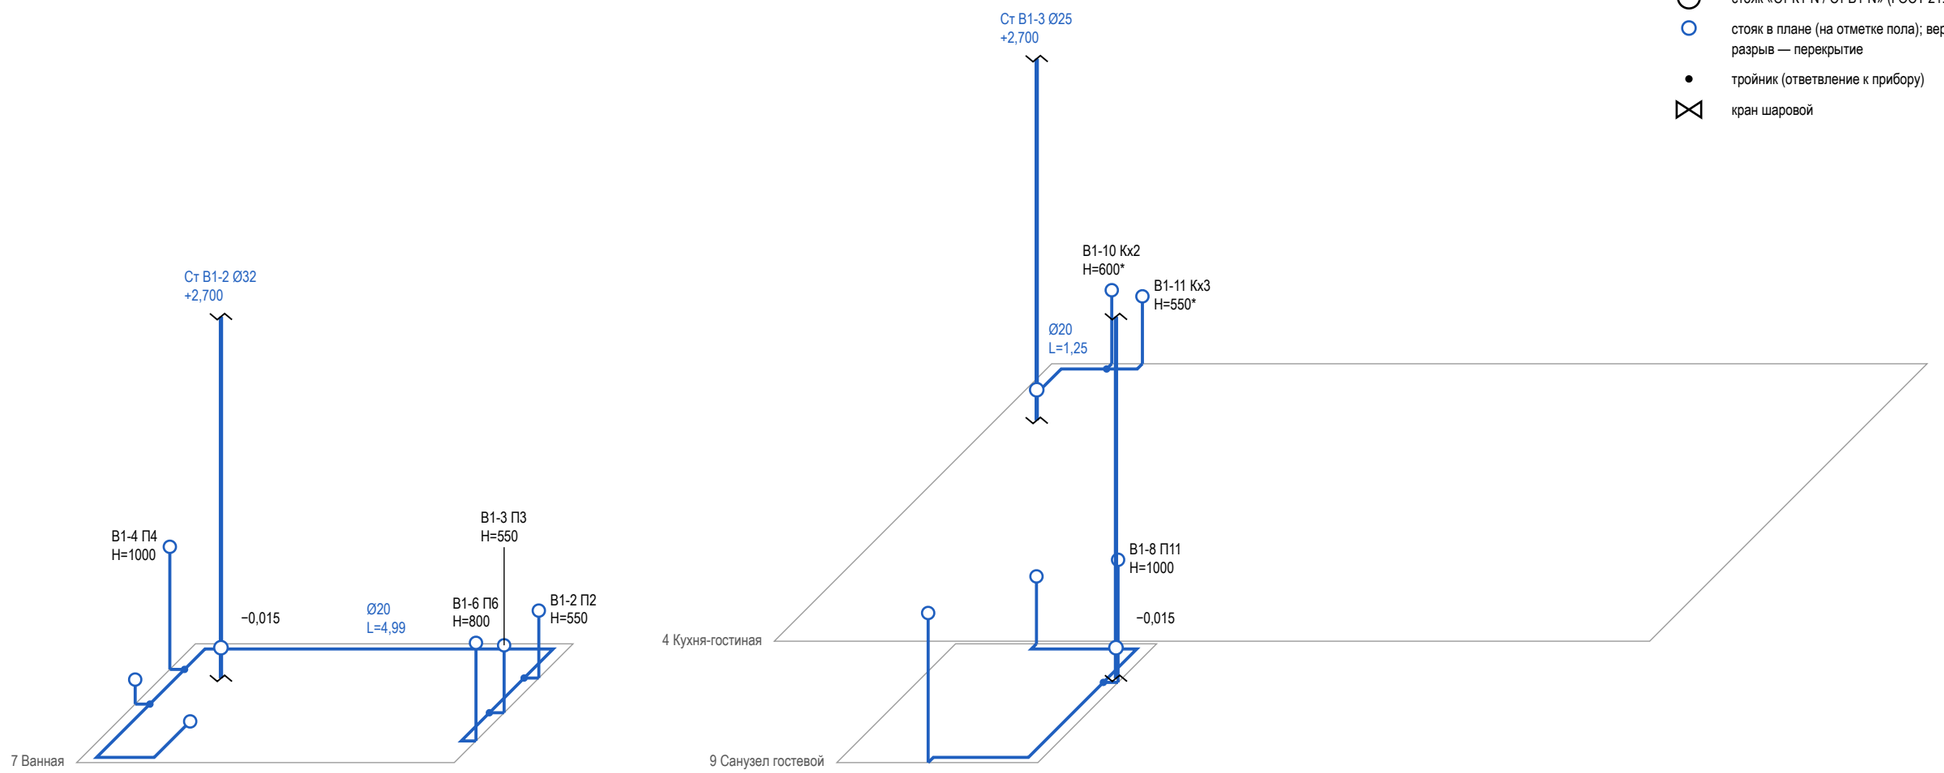

Допущения и предложения на листе

Основа листа: размеры сняты с растрового плана заказчика с частичными размерами: рисунок не в масштабе, помещения выровнены по подписанным размерам мебели и проходов; контрольный обмер не выполнен (К-1); высота потолка 2700 мм принята: на плане заказчика её нет (К-2); толщины стен 300 / 120 мм приняты по плану заказчика, не замерены (К-1); разрешённая мощность 15 кВт принята по типовым ТУ для квартиры, ТУ заказчиком не переданы (К-4); подрайон климата не задан — принят не северный (жилые от 2,5 м) (К-6).

Открытые вопросы и конфликты по листу: К-17.

См. лист открытых вопросов (лист 6, записи К-1, К-2, К-4, К-6; лист 7, запись К-17).

Примечания

1. Схема В1 построена по тем же трассам, что план разводки: положение в плане сохранено, глубина — в масштабе ×0,5. Трассы принципиальные; фактическое положение фиксируется исполнительной схемой до закрытия.
2. Высоты Н — от чистого пола помещения, мм. Прокладка магистрали В1 по данным: в стяжке пола, в стяжке пола, выше плиты перекрытия; отметка трасс — по пирогу пола.
3. * — высота вывода принята по практике монтажа; сверить по паспорту прибора.
4. Узел ввода В1 (кран, фильтр, счётчик, обратный клапан, кран) — на схеме разводки; состав узла ввода — по согласованию. Кран шаровой — на первом участке от стояка.
5. Трубы испытать давлением до закрытия (акт скрытых работ, опрессовка по СП 73.13330.2016).
6. Диаметры, высоты выводов и места кранов — по паспортам выбранных приборов и расчёту проектной организации.
7. Расчёт систем, диаметры магистралей и подбор оборудования выполняет проектная организация.

1000 мм · печать 1:1

Изм.	Кол.уч	Лист	№ док.	Подп.	Дата
Разраб.		Кырлан А.С.			04.11.26
Пров.					
ГИП					
Н. контр.					
Утв.					

ГД-2026-008-АИ

Квартира с кабинетом

Общая площадь 127,29* м² · * размеры со скана, не замерены (реестр — л. 6–8, К-1)

Дизайн-проект интерьера

Стадия	Лист	Листов
РП	38	131

Аксонометрическая схема В1 (холодное водоснабжение)

М 1:50

Кырлан Александр Сергеевич

выпуск 04.11.2026 № 4177cbe7a3 · стр. 43 из 166

Аксонометрическая схема Т3 (горячее водоснабжение)


аксонометрия · диаметры, уклоны, отметки, стояки и приборы · трассы принципиальные

Схема Т3 (М 1:50; по вертикали и горизонтали один масштаб, глубина — ×0,5 под 45°)

ПРЕДВАРИТЕЛЬНО · не для производства работ · открыто пунктов: 13 (реестр — л. 6–8)

Условные обозначения

- Т3 — горячее водоснабжение, подача (ГВС), PP-R Ø20
- вывод Т3 (код — в ведомости привязок)
- стояк «Ст К1-N / Ст В1-N» (ГОСТ 21.601), Ø мм
- стояк в плане (на отметке пола); вертикаль — стояк по высоте, разрыв — перекрытие
- тройник (ответвление к прибору)
- кран шаровой

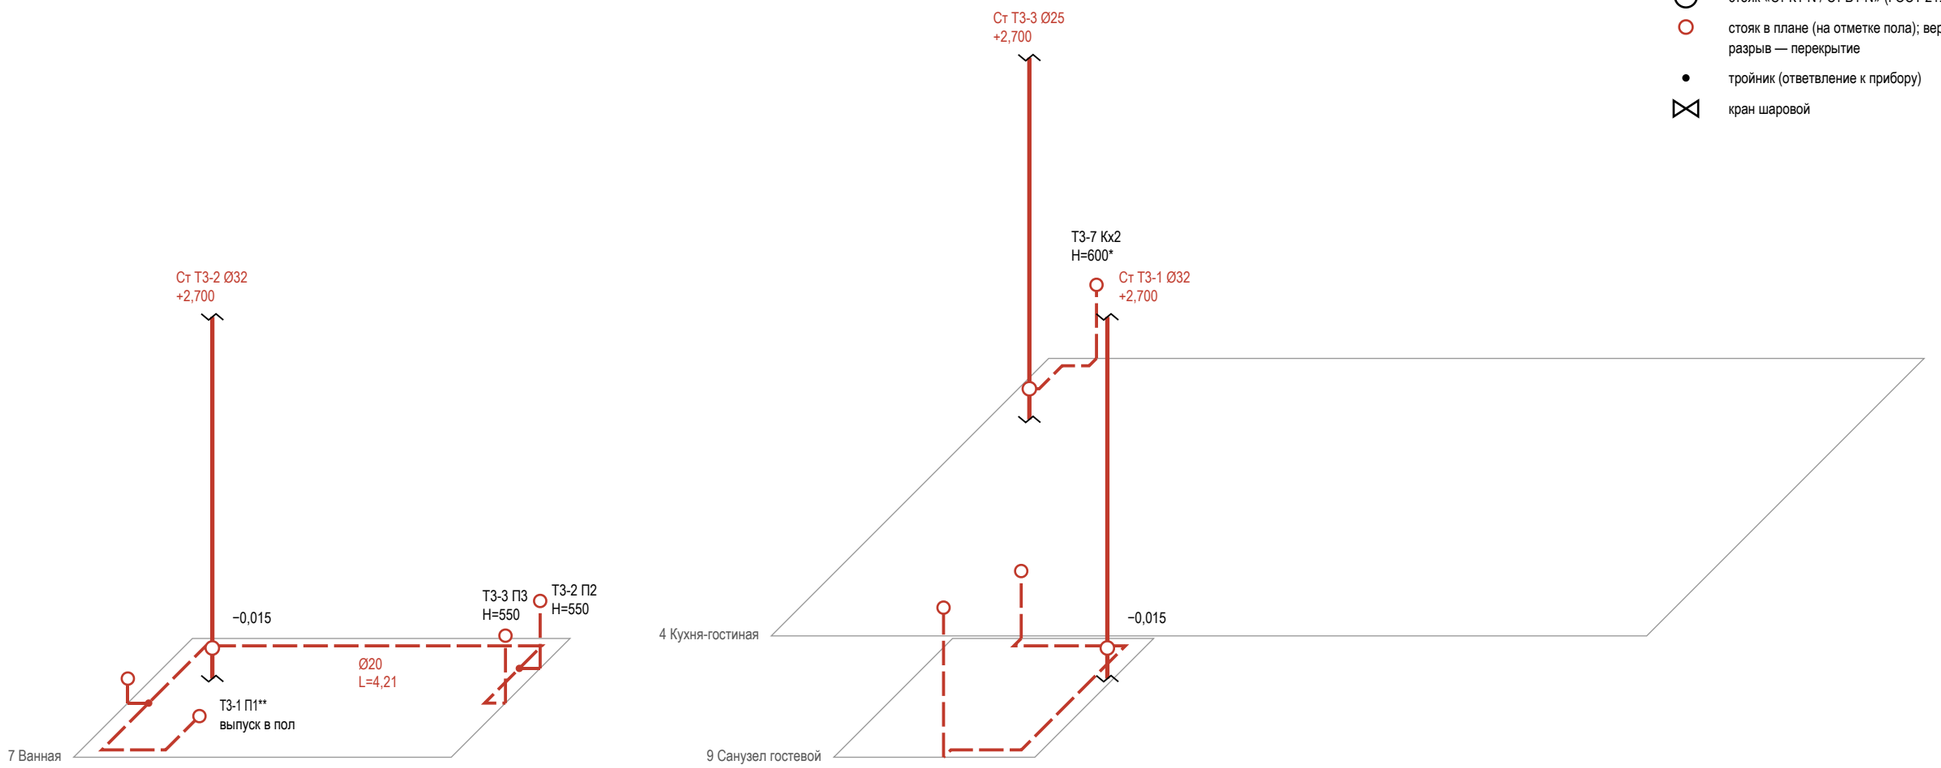

Допущения и предложения на листе

Основа листа: размеры сняты с растрового плана заказчика с частичными размерами: рисунок не в масштабе, помещения выровнены по подписанным размерам мебели и проходов; контрольный обмер не выполнен (К-1); высота потолка 2700 мм принята: на плане заказчика её нет (К-2); толщины стен 300 / 120 мм приняты по плану заказчика, не замерены (К-1); разрешённая мощность 15 кВт принята по типовым ТУ для квартиры, ТУ заказчиком не переданы (К-4); подрайон климата не задан — принят не северный (жилые от 2,5 м) (К-6).

Знак «**» — предложение проектировщика, заказчиком не утверждено (согласовать с заказчиком): К-11: П1 — Стойка смесителя и выводы ванны в полу — предложение проектировщика; пирог пола — К-11.

См. лист открытых вопросов (лист 6, записи К-1, К-2, К-4, К-6, К-11).

Примечания

1. Схема Т3 построена по тем же трассам, что план разводки: положение в плане сохранено, глубина — в масштабе ×0,5. Трассы принципиальные; фактическое положение фиксируется исполнительной схемой до закрытия.
2. Высоты Н — от чистого пола помещения, мм. Прокладка магистрали Т3 по данным: в стяжке пола, в стяжке пола, выше плиты перекрытия; отметка трасс — по пирогу пола.
3. * — высота вывода принята по практике монтажа; сверить по паспорту прибора.
4. Узел ввода Т3 (кран, фильтр, счётчик, обратный клапан, кран) — на схеме разводки; состав узла ввода — по согласованию. Кран шаровой — на первом участке от стояка.
5. Циркуляция ГВС в данных не задана — циркуляционного трубопровода на схеме нет (запись реестра К-17).
6. Трубы испытать давлением до закрытия (акт скрытых работ, опрессовка по СП 73.13330.2016).
7. Диаметры, высоты выводов и места кранов — по паспортам выбранных приборов и расчёту проектной организации.
8. Расчёт систем, диаметры магистралей и подбор оборудования выполняет проектная организация.

1000 мм · печать 1:1

Изм.	Кол.уч	Лист	№ док.	Подп.	Дата
Разраб.		Кырлан А.С.			04.11.26
Пров.					
ГИП					
Н. контр.					
Утв.					

ГД-2026-008-АИ

Квартира с кабинетом

Общая площадь 127,29* м² · * размеры со скана, не замерены (реестр — л. 6–8, К-1)

	Стадия	Лист	Листов
Дизайн-проект интерьера	РП	39	131

Аксонометрическая схема Т3 (горячее водоснабжение)

М 1:50

Кырлан Александр Сергеевич

выпуск 04.11.2026 № 4177cbe7a3 · стр. 44 из 166

Аксонометрическая схема К1 (канализация)


аксонометрия · диаметры, уклоны, отметки, стояки и приборы · трассы принципиальные

Схема К1 (М 1:50; по вертикали и горизонтали один масштаб, глубина — ×0,5 под 45°)

ПРЕДВАРИТЕЛЬНО · не для производства работ · открыто пунктов: 13 (реестр — л. 6–8)

Условные обозначения

- К1 — канализация бытовая
- вывод К1 (код — в ведомости привязок)
- стояк «Ст К1-N / Ст В1-N» (ГОСТ 21.601), Ø мм
- стояк в плане (на отметке пола); вертикаль — стояк по высоте, разрыв — перекрытие
- направление уклона К1 / пола: Ø, мм на 1 м
- ревизия (прочистка) К1 — доступ сохранить
- тройник (ответвление к прибору)

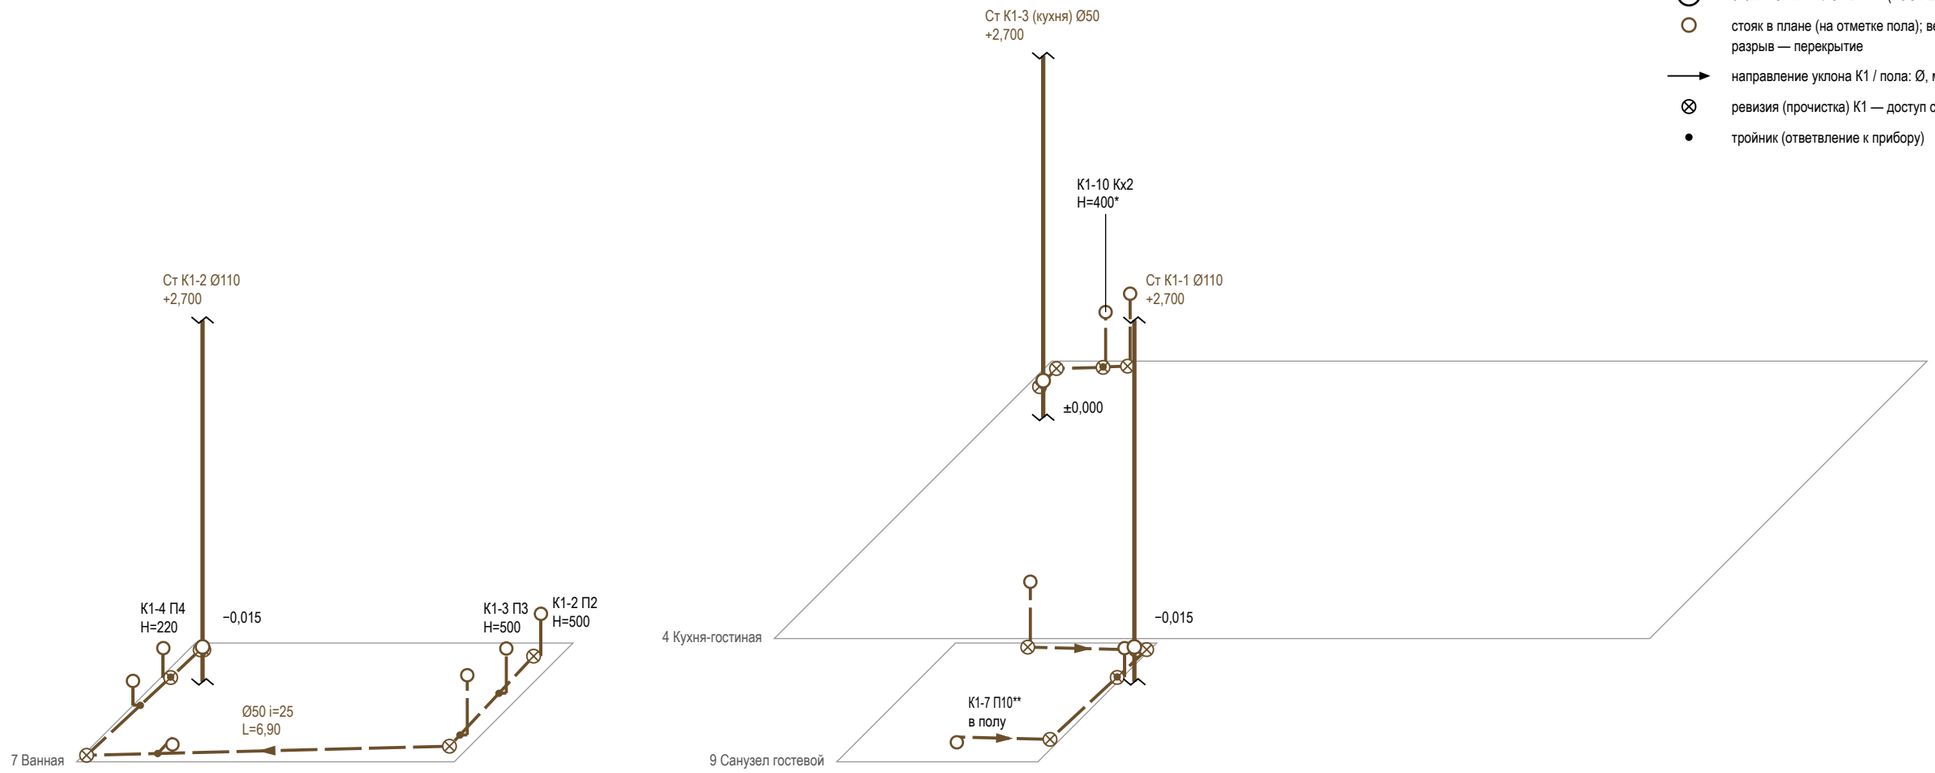

Допущения и предложения на листе

Основа листа: размеры сняты с растрового плана заказчика с частичными размерами: рисунок не в масштабе, помещения выровнены по подписанным размерам мебели и проходов; контрольный обмер не выполнен (К-1); высота потолка 2700 мм принята: на плане заказчика её нет (К-2); толщины стен 300 / 120 мм приняты по плану заказчика, не замерены (К-1); разрешённая мощность 15 кВт принята по типовым ТУ для квартиры, ТУ заказчиком не переданы (К-4); подрайон климата не задан — принят не северный (жилые от 2,5 м) (К-6).

Знак «**» — предложение проектировщика, заказчиком не утверждено (согласовать с заказчиком): К-10: П10 — Душевая зона 900 × 1640 у стены В и подиум 120 мм у трапа (ступень 127 мм) — предложение проектировщика: трап в стяжке 35 мм с облицовкой 14 мм не встаёт (монтажная высота трапа 90 до верха решётки + уклон отвода Ø50 до стояка 78 = 168 мм при врезке на уровне плиты); край подиума у проёма — вариант расстановки за автором.

См. лист открытых вопросов (лист 6, записи К-1, К-2, К-4, К-6, К-10).

Примечания

1. Схема К1 построена по тем же трассам, что план разводки: положение в плане сохранено, глубина — в масштабе ×0,5. Трассы принципиальные; фактическое положение фиксируется исполнительной схемой до закрытия.
2. Отметки — от плиты перекрытия: низ трубы у врезки в стояк — отметка из данных выпуска, к прибору труба поднимается на уклон i, мм/м (уклон не менее 1/d и не более 150 мм/м, СП 30.13330.2020, п. 19.1); чистый пол — выше плиты на стяжку (высота пирога пола). Высота выпуска прибора H — от чистого пола.
3. * — высота вывода принята по практике монтажа; сверить по паспорту прибора.
4. Ревизия — на повороте и в начале участка; стояк К1 в коробе с люком — звукоизоляция стояка в коробе; поворот — двумя отводами 45°.
5. Трубы испытать давлением до закрытия (акт скрытых работ, опрессовка по СП 73.13330.2016).
6. Диаметры, высоты выводов и места кранов — по паспортам выбранных приборов и расчёту проектной организации.
7. Расчёт систем, диаметры магистралей и подбор оборудования выполняет проектная организация.

1000 мм · печать 1:1

Изм.	Кол.уч	Лист	№ док.	Подп.	Дата
Разраб.		Кырлан А.С.			04.11.26
Пров.					
ГИП					
Н. контр.					
Утв.					

ГД-2026-008-АИ

Квартира с кабинетом

Общая площадь 127,29* м² · * размеры со скана, не замерены (реестр — л. 6–8, К-1)

Дизайн-проект интерьера	Стадия	Лист	Листов
	РП	40	131

Аксонометрическая схема К1 (канализация)

М 1:50

Кырлан Александр Сергеевич


выпуск 04.11.2026 № 4177cbe7a3 · стр. 45 из 166

Развёртки мокрых зон: выводы ВК. Кухня-гостиная

ПРЕДВАРИТЕЛЬНО · не для производства работ · открыто пунктов: 13 (реестр — л. 6–8)

пом. 4 · выводы В1, Т3, К1 на стенах · высоты от чистого пола, привязки от чистовых углов, мм

Стена А (М 1:25)

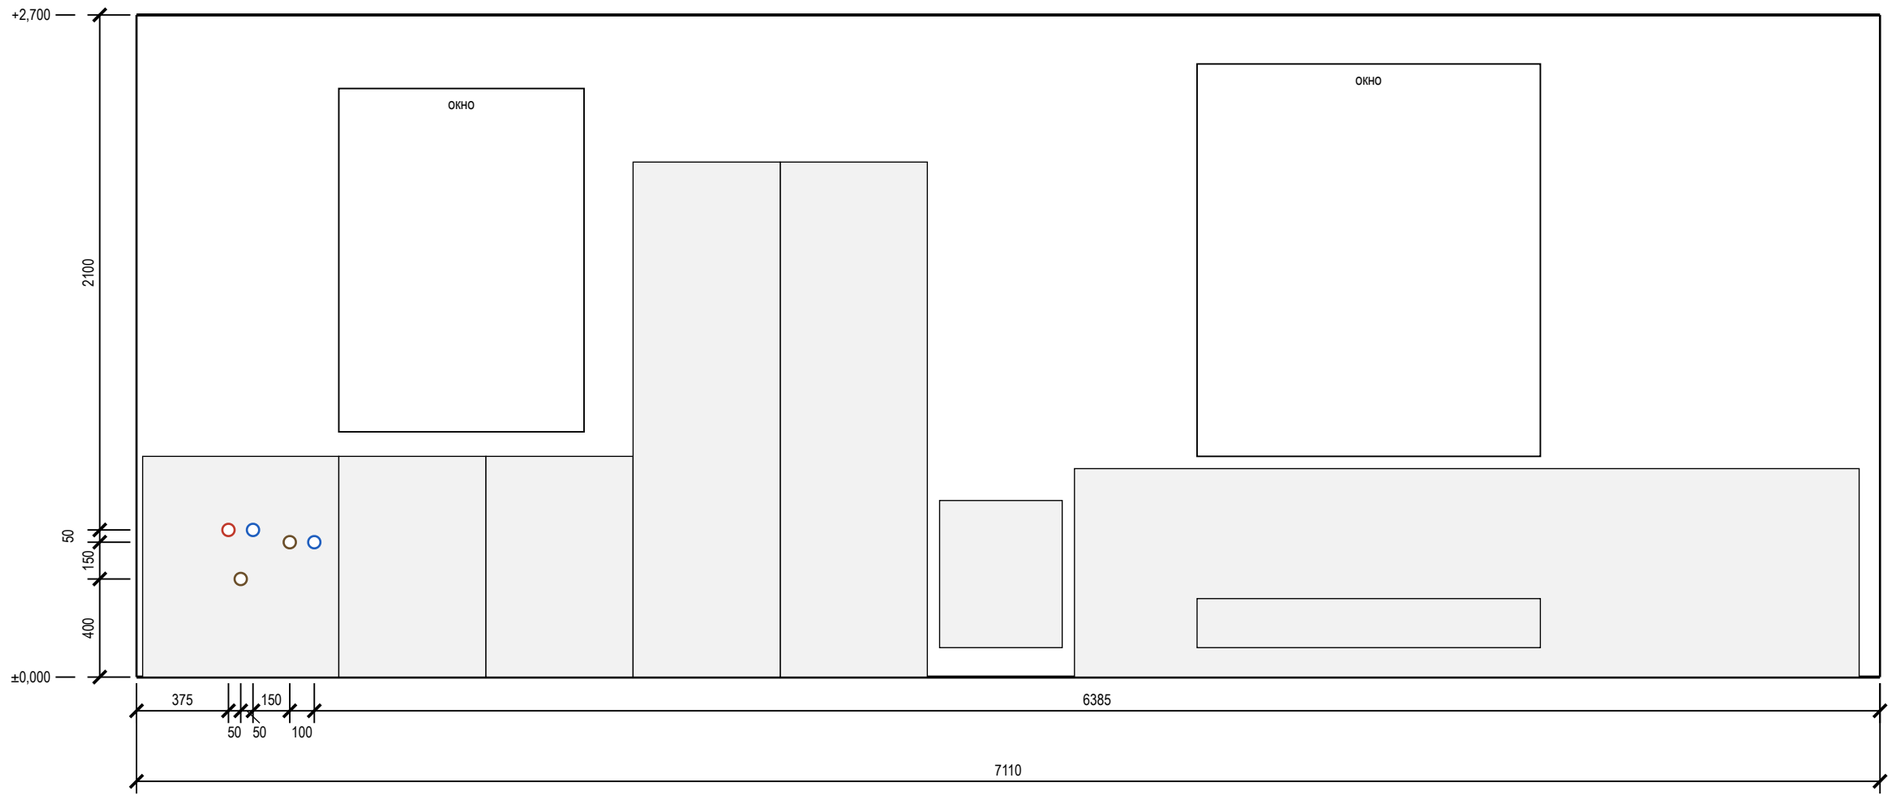

Ведомость привязок выводов (от чистого пола и угла)

Код	Прибор	Ø	Н, мм	Привязка, мм
В1-10	Кх2 мойка кухонная	½"	600*	ст. А: 475 от лев. угла
Т3-7	Кх2 мойка кухонная	½"	600*	ст. А: 375 от лев. угла
К1-10	Кх2 мойка кухонная	Ø50	400*	ст. А: 425 от лев. угла
В1-11	Кх3 посудомоечная машина	½"	550*	ст. А: 725 от лев. угла
К1-11	Кх3 посудомоечная машина	Ø40	550*	ст. А: 625 от лев. угла

Условные обозначения

- вывод В1 (код — в ведомости привязок)
- вывод Т3 (код — в ведомости привязок)
- вывод К1 (код — в ведомости привязок)
- сантехприбор по расстановке (габарит модели)
- дверной проём; окно — сплошной контур

Допущения и предложения на листе

Основа листа: размеры сняты с растрового плана заказчика с частичными размерами: рисунок не в масштабе, помещения выровнены по подписанным размерам мебели и проходов; контрольный обмер не выполнен (К-1); высота потолка 2700 мм принята: на плане заказчика её нет (К-2); толщины стен 300 / 120 мм приняты по плану заказчика, не замерены (К-1); разрешённая мощность 15 кВт принята по типовым ТУ для квартиры, ТУ заказчиком не переданы (К-4); подрайон климата не задан — принят не северный (жилые от 2,5 м) (К-6).

Открытые вопросы и конфликты по листу: К-17.

См. лист открытых вопросов (лист 6, записи К-1, К-2, К-4, К-6; лист 7, запись К-17).

Примечания

1. Габариты и высоты приборов, межосевые смесителей и места кранов — по паспортам выбранных приборов, сверяются до разметки стен.
2. Высоты Н — от чистого пола помещения, мм; отметка чистого пола и потолка — у левого края вида (от ±0,000 объекта). Привязки — от левого чистового угла вида (облицовка стен вычтена), как на развёртках стен.
3. * — высота принята по практике монтажа: в данных прибора её нет; до разметки стен сверить по паспорту выбранного прибора (смеситель, инсталляция, сифон).
4. Стояки в помещении: Ст К1-3 (кухня) Ø50, Ст В1-3 Ø25, Ст Т3-3 Ø25 — положение на плане выводов; выводы подключаются к ним по схеме разводки.
5. Ревизионные люки (арматура и ревизии у Кх2, Кх3 300×400, стена А у Кх2, предложение): привязка к углу — по раскладке плитки, подтверждается обмером.
6. Ревизионные люки к арматуре и ревизиям в данных не заданы: место и размер не определены (записи реестра нет).
7. Мойка, ПММ и фильтр — выводы в шкафу мойки; диаметры и положение сифона и кранов сверить по паспортам приборов и чертежам модуля.
8. Часть подписей выводов не уместилась у знака: коды и высоты — в ведомости привязок.
9. Расчёт систем водоснабжения и канализации и подбор оборудования выполняет проектная организация; лист задаёт места и высоты выводов.

1000 мм · печать 1:1

Изм.	Кол.уч	Лист	№ док.	Подп.	Дата
Разраб.		Кырлан А.С.			04.11.26
Пров.					
ГИП					
Н. контр.					
Утв.					

ГД-2026-008-АИ

Квартира с кабинетом

Общая площадь 127,29* м² · * размеры со скана, не замерены (реестр — л. 6–8, К-1)

Дизайн-проект интерьера

Стадия	Лист	Листов
РП	41	131

Развёртки мокрых зон: выводы ВК. Кухня-гостиная

М 1:25


Кырлан Александр Сергеевич

выпуск 04.11.2026 № 4177cbe7a3 · стр. 46 из 166


Развёртки мокрых зон: выводы ВК. Ванная (лист 1 из 2)

пом. 7 · выводы В1, Т3, К1 на стенах · высоты от чистого пола, привязки от чистовых углов, мм

Стена А (М 1:20)

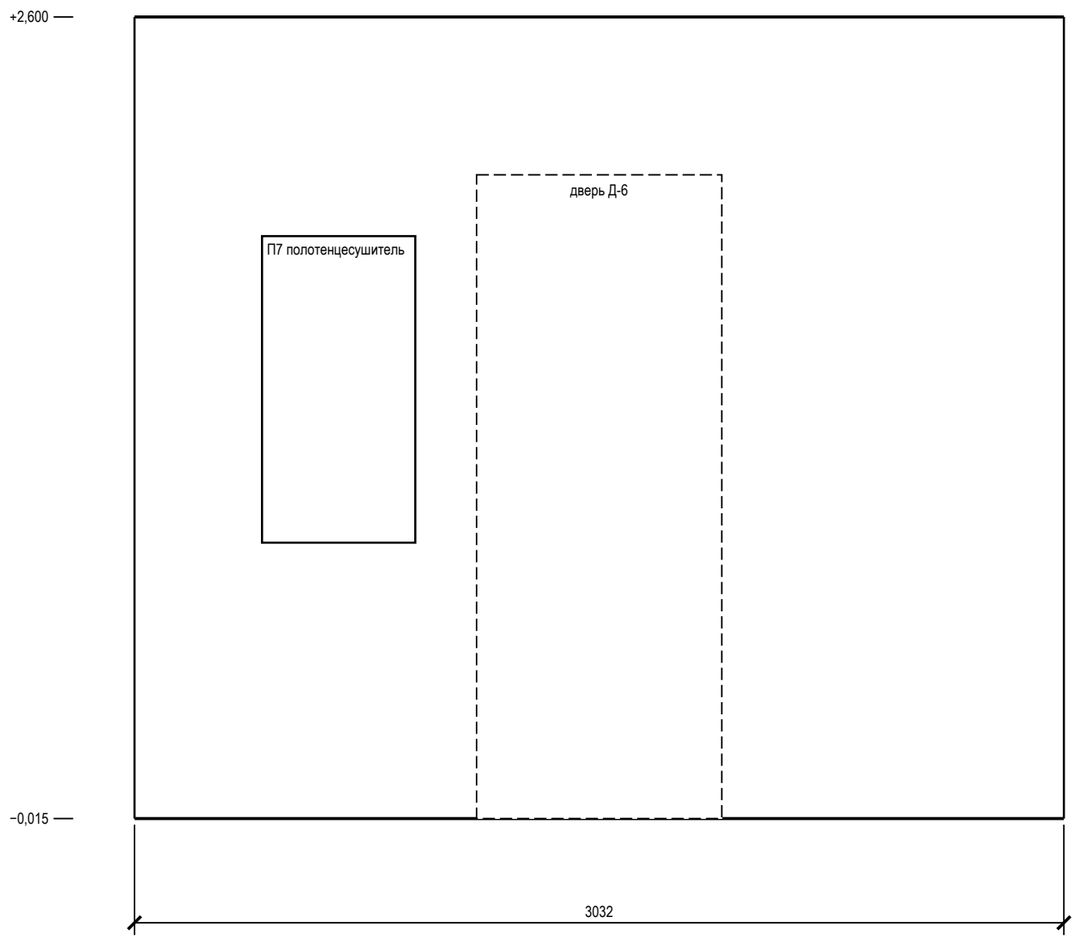

Стена Б (М 1:20)

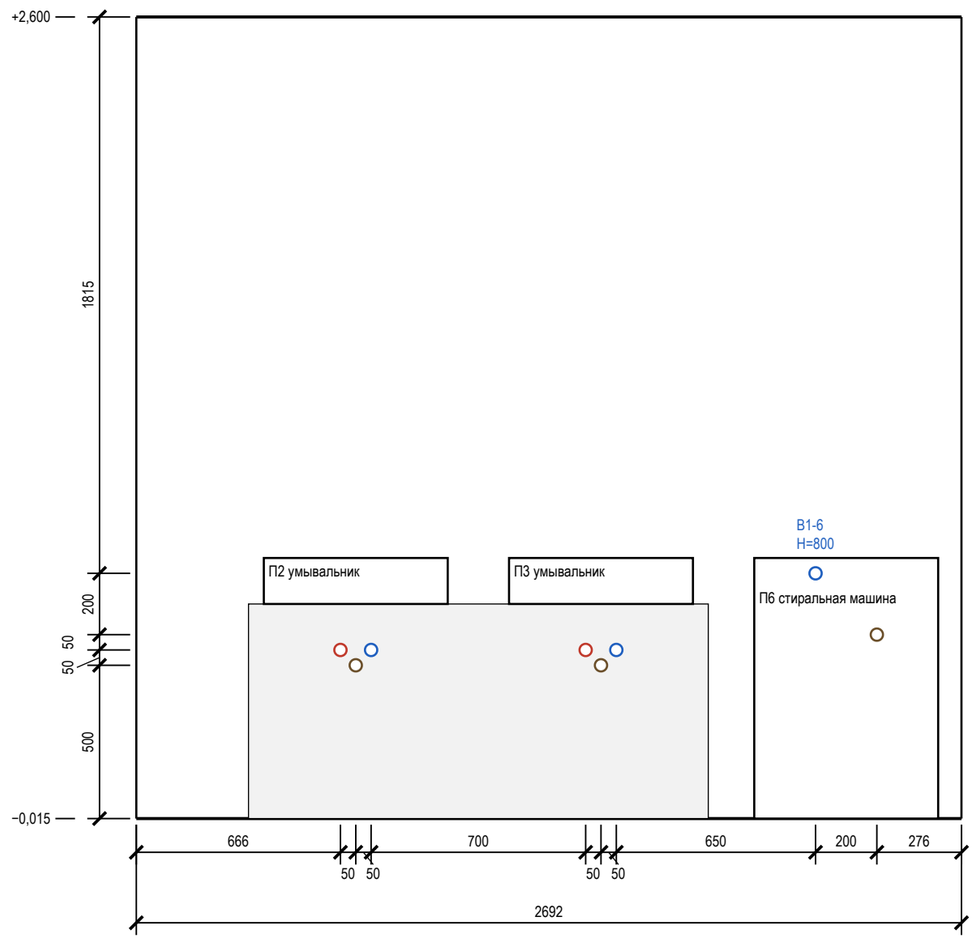

Ведомость привязок выводов (от чистого пола и угла)

Код	Прибор	Ø	Н, мм	Привязка, мм
В1-2	П2 умывальник	½"	550	ст. Б: 766 от лев. угла
Т3-2	П2 умывальник	½"	550	ст. Б: 666 от лев. угла
К1-2	П2 умывальник	Ø50	500	ст. Б: 716 от лев. угла
В1-3	П3 умывальник	½"	550	ст. Б: 1566 от лев. угла

Ведомость привязок (продолжение)

Код	Прибор	Ø	Н, мм	Привязка, мм
Т3-3	П3 умывальник	½"	550	ст. Б: 1466 от лев. угла
К1-3	П3 умывальник	Ø50	500	ст. Б: 1516 от лев. угла
В1-6	П6 стиральная машина	½"	800	ст. Б: 2216 от лев. угла
К1-6	П6 стиральная машина	Ø50	600	ст. Б: 2416 от лев. угла

Условные обозначения

- вывод В1 (код — в ведомости привязок)
- вывод Т3 (код — в ведомости привязок)
- вывод К1 (код — в ведомости привязок)
- сантехприбор по расстановке (габарит модели)
- дверной проём; окно — сплошной контур

Допущения и предложения на листе. Знак «**» предложено (согласовать): дверь пом. 7 (стена А). См. лист открытых вопросов (листы 6–8).

Примечания

1. Габариты и высоты приборов, межосевые смесителей и места кранов — по паспортам выбранных приборов, сверяются до разметки стен.
2. Высоты Н — от чистого пола помещения, мм; отметка чистого пола и потолка — у левого края вида (от ±0,000 объекта). Привязки — от левого чистового угла вида (облицовка стен вычтена), как на развёртках стен.
3. Выводы в полу (В1-1, Т3-1, К1-1): трап, лоток, выпуск отдельностоящей ванны, подвод к стойке напольного смесителя — на развёртке их нет; место и пирог пола — лист «Схема разводки» (профиль К1, узел 1).
4. Стояки в помещении: Ст К1-2 Ø110, Ст В1-2 Ø32, Ст Т3-2 Ø32 — положение на плане выводов; выводы подключаются к ним по схеме разводки.
5. Ревизионные люки (арматура и ревизии у П1** 300×400, стена В у П1**, предложение): привязка к углу — по раскладке плитки, подтверждается обмером.
6. Ревизионные люки к арматуре и ревизиям в данных не заданы: место и размер не определены (записи реестра нет).
7. Часть подписей выводов не уместилась у знака: коды и высоты — в ведомости привязок.
8. Помещение «Ванная» — 2 листа: стены 1) А, Б; 2) В, Г.
9. Расчёт систем водоснабжения и канализации и подбор оборудования выполняет проектная организация; лист задаёт места и высоты выводов.

1000 мм · печать 1:1

Изм.	Кол.уч	Лист	№ док.	Подп.	Дата
Разраб.		Кырлан А.С.			04.11.26
Пров.					
ГИП					
Н. контр.					
Утв.					

ГД-2026-008-АИ

Квартира с кабинетом

Общая площадь 127,29* м² · * размеры со скана, не замерены (реестр — л. 6–8, К-1)

Дизайн-проект интерьера

Стадия	Лист	Листов
РП	42	131

Развёртки мокрых зон: выводы ВК. Ванная (лист 1 из 2)

М 1:20

Кырлан Александр Сергеевич


выпуск 04.11.2026 № 4177cbe7a3 · стр. 47 из 166

Развёртки мокрых зон: выводы ВК. Ванная (лист 2 из 2)


пом. 7 · выводы В1, Т3, К1 на стенах · высоты от чистого пола, привязки от чистовых углов, мм

ПРЕДВАРИТЕЛЬНО · не для производства работ · открыто пунктов: 13 (реестр — л. 6–8)

Стена В (М 1:20)

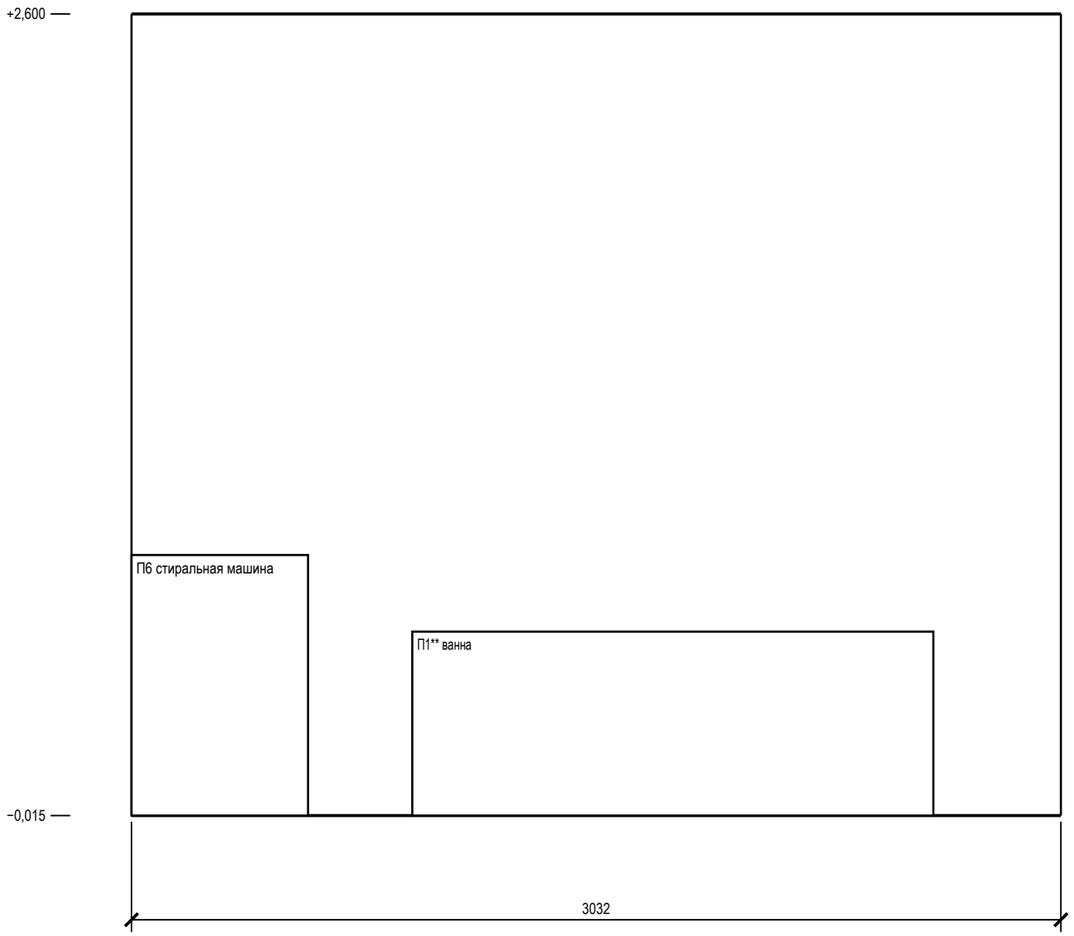

Стена Г (М 1:20)

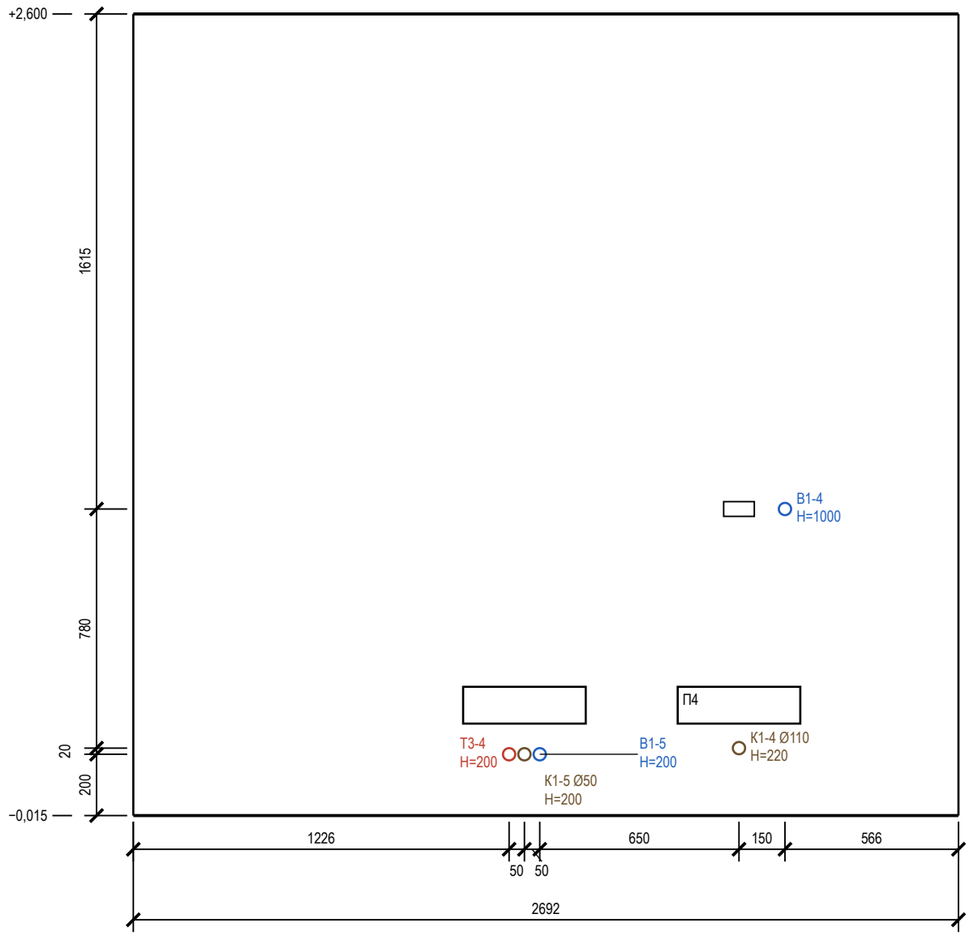

Ведомость привязок выводов (от чистого пола и угла)

Код	Прибор	Ø	Н, мм	Привязка, мм
В1-4	П4 унитаз подвесной	½"	1000	ст. Г: 2126 от лев. угла
К1-4	П4 унитаз подвесной	Ø110	220	ст. Г: 1976 от лев. угла
В1-5	П5 биде подвесное	½"	200	ст. Г: 1326 от лев. угла

Ведомость привязок (продолжение)

Код	Прибор	Ø	Н, мм	Привязка, мм
Т3-4	П5 биде подвесное	½"	200	ст. Г: 1226 от лев. угла
К1-5	П5 биде подвесное	Ø50	200	ст. Г: 1276 от лев. угла

Условные обозначения

- вывод В1 (код — в ведомости привязок)
- вывод Т3 (код — в ведомости привязок)
- вывод К1 (код — в ведомости привязок)
- сантехприбор по расстановке (габарит модели)
- дверной проём; окно — сплошной контур
- кнопка смыва инсталляции (Н — по данным прибора)

Допущения и предложения на листе. Основа листа: размеры сняты с растрового плана заказчика с частичными размерами: рисунок не в масштабе, помещения выровнены по подписанным размерам мебели и проходов; контрольный обмер не выполнен (К-1); высота потолка 2700 мм принята: на плане заказчика её нет (К-2); толщины стен 300 / 120 мм приняты по плану заказчика, не замерены (К-1); разрешённая мощность 15 кВт принята по типовым ТУ для квартиры, ТУ заказчиком не переданы (К-4); подрайон климата не задан — принят не северный (жилые от 2,5 м) (К-6). Знак «**» — предложено, не утверждено (согласовать): К-11: П1. См. лист открытых вопросов (лист 6, записи К-1, К-2, К-4, К-6, К-11; лист 7, запись К-17).

Примечания

1. Габариты и высоты приборов, межосевые смесителей и места кранов — по паспортам выбранных приборов, сверяются до разметки стен.
2. Высоты Н — от чистого пола помещения, мм; отметка чистого пола и потолка — у левого края вида (от ±0,000 объекта). Привязки — от левого чистового угла вида (облицовка стен вычтена), как на развёртках стен.
3. Кнопка смыва П4 — Н=1000 (по данным прибора).
4. Выводы в полу (В1-1, Т3-1, К1-1): трап, лоток, выпуск отдельностоящей ванны, подвод к стойке напольного смесителя — на развёртке их нет; место и пирог пола — лист «Схема разводки» (профиль К1, узел 1).
5. Стояки в помещении: Ст К1-2 Ø110, Ст В1-2 Ø32, Ст Т3-2 Ø32 — положение на плане выводов; выводы подключаются к ним по схеме разводки.
6. Ревизионные люки (арматура и ревизии у П1** 300×400, стена В у П1**, предложение): привязка к углу — по раскладке плитки, подтверждается обмером.
7. Ревизионные люки к арматуре и ревизиям в данных не заданы: место и размер не определены (записи реестра нет).
8. Помещение «Ванная» — 2 листа: стены 1) А, Б; 2) В, Г.
9. Расчёт систем водоснабжения и канализации и подбор оборудования выполняет проектная организация; лист задаёт места и высоты выводов.

1000 мм · печать 1:1

Изм.	Кол.уч	Лист	№ док.	Подп.	Дата
Разраб.		Кырлан А.С.			04.11.26
Пров.					
ГИП					
Н. контр.					
Утв.					

ГД-2026-008-АИ

Квартира с кабинетом

Общая площадь 127,29* м² · * размеры со скана, не замерены (реестр — л. 6–8, К-1)

Дизайн-проект интерьера

Стадия	Лист	Листов
РП	43	131

Развёртки мокрых зон: выводы ВК. Ванная
(лист 2 из 2)
М 1:20

Кырлан Александр Сергеевич


выпуск 04.11.2026 № 4177cbe7a3 · стр. 48 из 166

Развёртки мокрых зон: выводы ВК. Санузел гостевой (лист 1 из 2)


пом. 9 · выводы В1, Т3, К1 на стенах · высоты от чистого пола, привязки от чистовых углов, мм

ПРЕДВАРИТЕЛЬНО · не для производства работ · открыто пунктов: 13 (реестр — л. 6–8)

Стена А (М 1:20)

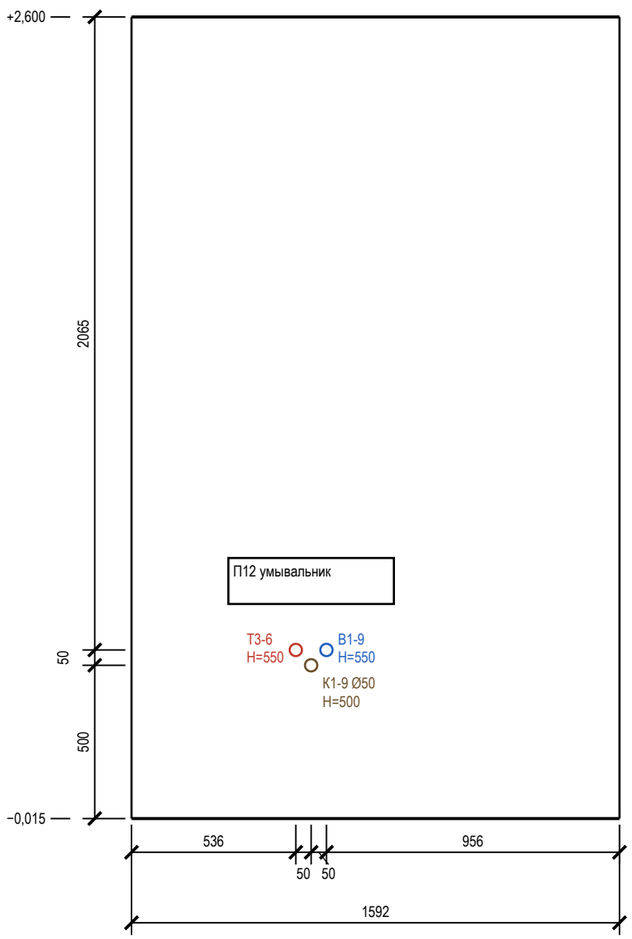

Стена Б (М 1:20)

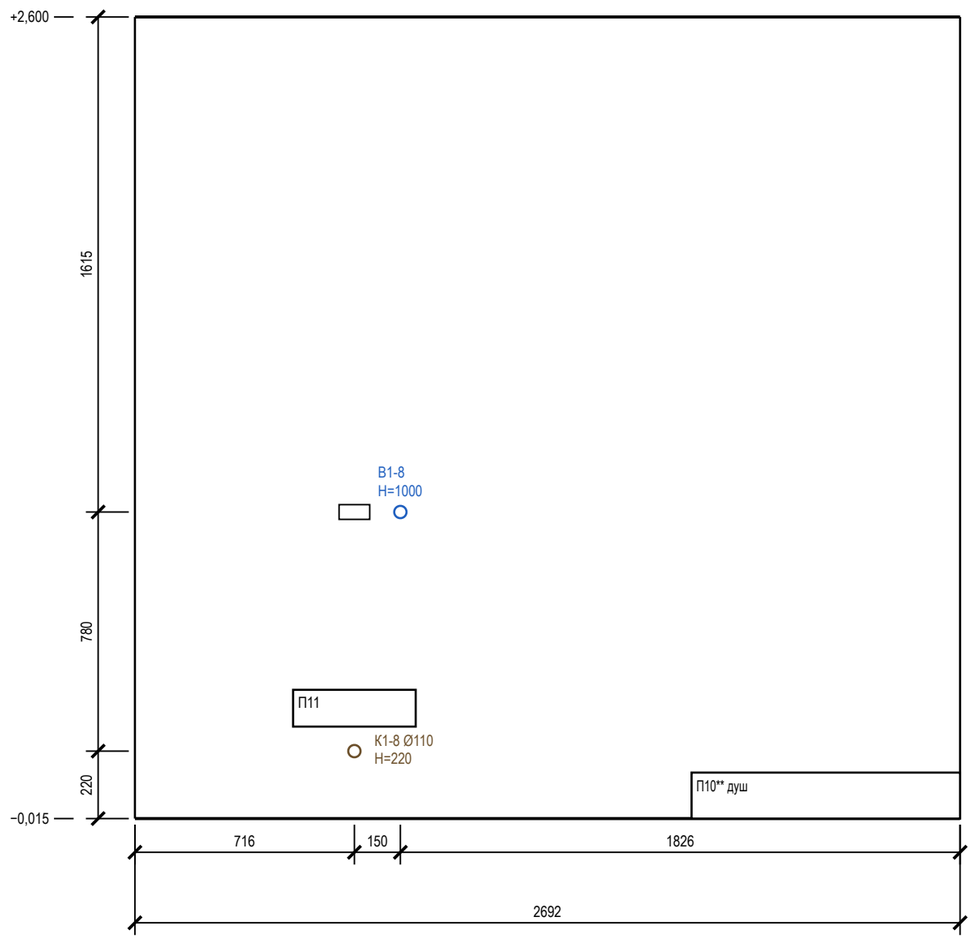

Допущения и предложения на листе

Основа листа: размеры сняты с растрового плана заказчика с частичными размерами: рисунок не в масштабе, помещения выровнены по подписанным размерам мебели и проходов; контрольный обмер не выполнен (К-1); высота потолка 2700 мм принята: на плане заказчика её нет (К-2); толщины стен 300 / 120 мм приняты по плану заказчика, не замерены (К-1); разрешённая мощность 15 кВт принята по типовым ТУ для квартиры, ТУ заказчиком не переданы (К-4); подрайон климата не задан — принят не северный (жилые от 2,5 м) (К-6).

Знак «**» — предложение проектировщика, заказчиком не утверждено (согласовать с заказчиком): К-10: П10 — Душевая зона 900 × 1640 у стены В и подиум 120 мм у трапа (ступень 127 мм) — предложение проектировщика: трап в стяжке 35 мм с облицовкой 14 мм не встаёт (монтажная высота трапа 90 до верха решётки + уклон отвода Ø50 до стояка 78 = 168 мм при врезке на уровне плиты); край подиума у проёма — вариант расстановки за автором.

Открытые вопросы и конфликты по листу: К-17.

См. лист открытых вопросов (лист 6, записи К-1, К-2, К-4, К-6, К-10; лист 7, запись К-17).

Ведомость привязок выводов (от чистого пола и угла)

Код	Прибор	Ø	H, мм	Привязка, мм
В1-9	П12 умывальник	½"	550	ст. А: 636 от лев. угла
Т3-6	П12 умывальник	½"	550	ст. А: 536 от лев. угла
К1-9	П12 умывальник	Ø50	500	ст. А: 586 от лев. угла

Ведомость привязок (продолжение)

Код	Прибор	Ø	H, мм	Привязка, мм
В1-8	П11 унитаз подвесной	½"	1000	ст. Б: 866 от лев. угла
К1-8	П11 унитаз подвесной	Ø110	220	ст. Б: 716 от лев. угла

Условные обозначения

- вывод В1 (код — в ведомости привязок)
- вывод Т3 (код — в ведомости привязок)
- вывод К1 (код — в ведомости привязок)
- сантехприбор по расстановке (габарит модели)
- дверной проём; окно — сплошной контур
- кнопка смыва инсталляции (H — по данным прибора)

Примечания

1. Габариты и высоты приборов, межосевые смесителей и места кранов — по паспортам выбранных приборов, сверяются до разметки стен.
2. Высоты H — от чистого пола помещения, мм; отметка чистого пола и потолка — у левого края вида (от ±0,000 объекта). Привязки — от левого чистового угла вида (облицовка стен вычтена), как на развёртках стен.
3. Кнопка смыва П11 — H=1000 (по данным прибора).
4. Выводы в полу (К1-1): трап, лоток, выпуск отдельностоящей ванны, подвод к стойке напольного смесителя — на развёртке их нет; место и пирог пола лист «Схема разводки» (профиль К1, узел 1).
5. Стояки в помещении: Ст К1-1 Ø110, Ст В1-1 Ø32, Ст Т3-1 Ø32 — положение на плане выводов; выводы подключаются к ним по схеме разводки.
6. Ревизионные люки (арматура и ревизии у П10** 300×400, стена В у П10**, предложение): привязка к углу — по раскладке плитки, подтверждается обмером.
7. Ревизионные люки к арматуре и ревизиям в данных не заданы: место и размер не определены (записи реестра нет).
8. Помещение «Санузел гостевой» — 2 листа: стены 1) А, Б; 2) В, Г.
9. Расчёт систем водоснабжения и канализации и подбор оборудования выполняет проектная организация; лист задаёт места и высоты выводов.

1000 мм · печать 1:1

Изм.	Кол.уч	Лист	№ док.	Подп.	Дата
Разраб.		Кырлан А.С.			04.11.26
Пров.					
ГИП					
Н. контр.					
Утв.					

ГД-2026-008-АИ

Квартира с кабинетом

Общая площадь 127,29* м² · * размеры со скана, не замерены (реестр — л. 6–8, К-1)

Дизайн-проект интерьера

Стадия	Лист	Листов
РП	44	131

Развёртки мокрых зон: выводы ВК. Санузел гостевой (лист 1 из 2)

М 1:20

Кырлан Александр Сергеевич


выпуск 04.11.2026 № 4177cbe7a3 · стр. 49 из 166

Развёртки мокрых зон: выводы ВК. Санузел гостевой (лист 2 из 2)


пом. 9 · выводы В1, Т3, К1 на стенах · высоты от чистого пола, привязки от чистовых углов, мм

ПРЕДВАРИТЕЛЬНО · не для производства работ · открыто пунктов: 13 (реестр — л. 6–8)

Стена В (М 1:20)

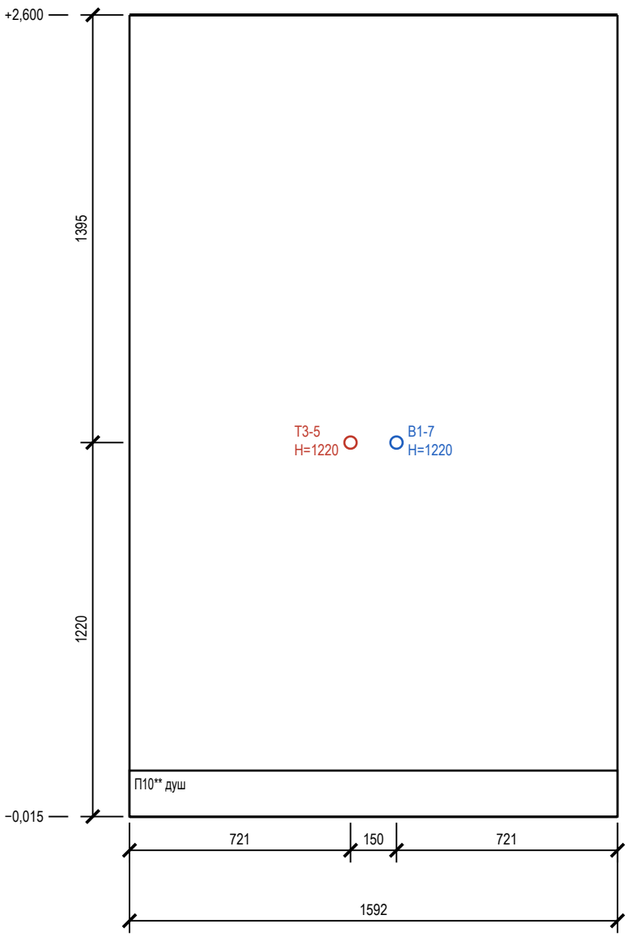

Стена Г (М 1:20)

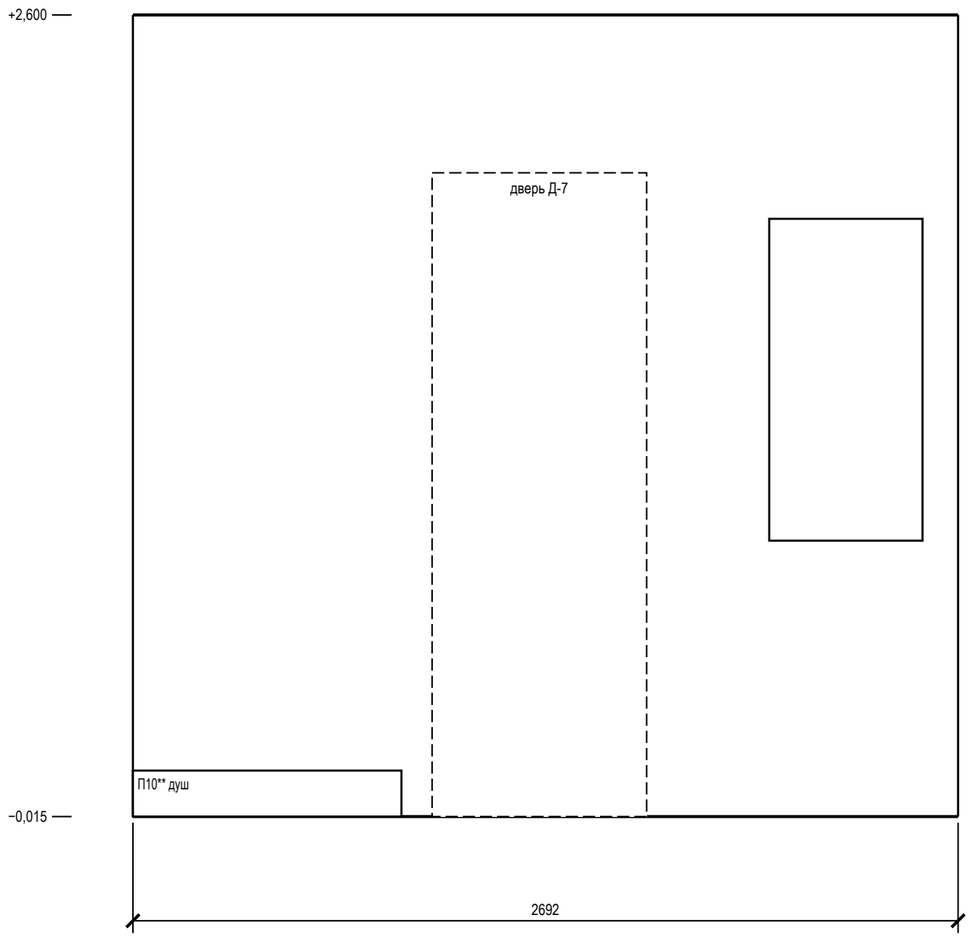

Допущения и предложения на листе

Основа листа: размеры сняты с растрового плана заказчика с частичными размерами: рисунок не в масштабе, помещения выровнены по подписанным размерам мебели и проходов; контрольный обмер не выполнен (К-1); высота потолка 2700 мм принята: на плане заказчика её нет (К-2); толщины стен 300 / 120 мм приняты по плану заказчика, не замерены (К-1); разрешённая мощность 15 кВт принята по типовым ТУ для квартиры, ТУ заказчиком не переданы (К-4); подрайон климата не задан — принят не северный (жилые от 2,5 м) (К-6).

Знак «**» — предложение проектировщика, заказчиком не утверждено (согласовать с заказчиком): К-10: П10 — Душевая зона 900 × 1640 у стены В и подиум 120 мм у трапа (ступень 127 мм) — предложение проектировщика: трап в стяжке 35 мм с облицовкой 14 мм не встаёт (монтажная высота трапа 90 до верха решётки + уклон отвода Ø50 до стояка 78 = 168 мм при врезке на уровне плиты); край подиума у проёма — вариант расстановки за автором.

См. лист открытых вопросов (лист 6, записи К-1, К-2, К-4, К-6, К-10).

Ведомость привязок выводов (от чистого пола и угла)

Код	Прибор	Ø	H, мм	Привязка, мм
В1-7	П10** душ	½"	1220	ст. В: 871 от лев. угла
Т3-5	П10** душ	½"	1220	ст. В: 721 от лев. угла

Условные обозначения

- вывод В1 (код — в ведомости привязок)
- вывод Т3 (код — в ведомости привязок)
- вывод К1 (код — в ведомости привязок)
- сантехприбор по расстановке (габарит модели)
- дверной проём; окно — сплошной контур

Примечания

1. Габариты и высоты приборов, межосевые смесителей и места кранов — по паспортам выбранных приборов, сверяются до разметки стен.
2. Высоты H — от чистого пола помещения, мм; отметка чистого пола и потолка — у левого края вида (от ±0,000 объекта). Привязки — от левого чистового угла вида (облицовка стен вычтена), как на развёртках стен.
3. Выводы в полу (К1-1): трап, лоток, выпуск отдельностоящей ванны, подвод к стойке напольного смесителя — на развёртке их нет; место и пирог пола лист «Схема разводки» (профиль К1, узел 1).
4. Стояки в помещении: Ст К1-1 Ø110, Ст В1-1 Ø32, Ст Т3-1 Ø32 — положение на плане выводов; выводы подключаются к ним по схеме разводки.
5. Ревизионные люки (арматура и ревизии у П10** 300×400, стена В у П10**, предложение): привязка к углу — по раскладке плитки, подтверждается обмером.
6. Ревизионные люки к арматуре и ревизиям в данных не заданы: место и размер не определены (записи реестра нет).
7. Помещение «Санузел гостевой» — 2 листа: стены 1) А, Б; 2) В, Г.
8. Расчёт систем водоснабжения и канализации и подбор оборудования выполняет проектная организация; лист задаёт места и высоты выводов.

1000 мм · печать 1:1

Изм.	Кол.уч	Лист	№ док.	Подп.	Дата
Разраб.		Кырлан А.С.			04.11.26
Пров.					
ГИП					
Н. контр.					
Утв.					

ГД-2026-008-АИ

Квартира с кабинетом

Общая площадь 127,29* м² · * размеры со скана, не замерены (реестр — л. 6–8, К-1)

Дизайн-проект интерьера

Стадия	Лист	Листов
РП	45	131

Развёртки мокрых зон: выводы ВК. Санузел гостевой (лист 2 из 2)

М 1:20

Кырлан Александр Сергеевич

выпуск 04.11.2026 № 4177cbe7a3 · стр. 50 из 166

Спецификация сантехнического оборудования

Форма 1 ГОСТ 21.110-2013 · ГД-2026-008-АИ-ВК.СО · приборы, арматура, трубопроводы

ПРЕДВАРИТЕЛЬНО · не для производства работ · открыто пунктов: 13 (реестр — л. 6–8)

Поз.	Наименование и техническая характеристика	Тип, марка, обозначение документа	Код продукции	Поставщик	Ед. изм.	Кол.	Масса 1 ед., кг	Примечание
	Санитарные приборы							
1	Ванна отдельностоящая из литого камня 1700×800 мм, выпуск в пол; донный клапан, перелив и сифон отдельной позицией Допущения и предложения на листе. Знак «**» предложено (согласовать). См. лист открытых вопросов (листы 6–8).	ванна отдельностоящая овальная 1700×800, литой камень; смеситель напольный		выбор заказчика	шт	1		П1**
2	Унитаз подвесной безободковый, с сиденьем микролифт, крепёж и звукоизолирующая прокладка	Jacob Delafon Struktura EDF102-00		выбор заказчика	шт	2		П4, П11
3	Инсталляция для подвесного унитаза: рама высотой 1120 мм, бачок, клавиша смыва (ось клавиши 1050 мм от чистого пола)	аналог		выбор заказчика	шт	2		П4 — короб ГКЛВ общий с П5; П11 короб ГКЛВ
4	Раковина накладная 600×450 мм, на столешницу тумбы, с переливом	раковина накладная овальная, две на тумбе 1500		выбор заказчика	шт	2		П2, П3
5	Умывальник из травертина 540×400 мм на консоли, с переливом	раковина 540 на консоли, травертин		выбор заказчика	шт	1		П12
6	Биде подвесное, крепёж и звукоизолирующая прокладка	биде подвесное		выбор заказчика	шт	1		П5
7	Инсталляция для подвесного биде: рама с крепёжными шпильками, водорозетками ½" (ХВ, ГВ) и выпуском Ø50	аналог		выбор заказчика	шт	1		П5; короб ГКЛВ общий с П4
8	Трап душевой с гидрозатвором и фланцем под гидроизоляцию, монтажная высота по паспорту	аналог		выбор заказчика	шт	1		П10**; узел 1 схема разводки
9	Мойка кухонная врезная / подстольная, с переливом, ориентир 700×480 мм — в модуле Кх2 шириной 800 мм, вырез по шаблону модели	аналог		с кухонной мебелью	шт	1		Кх2
10	Полотенцесушитель электрический, IP44, с терморегулятором	аналог		выбор заказчика	шт	2		П7, П13**
	Смесители, сифоны и арматура приборов							
11	Смеситель для ванны напольный (стойка) однорычажный, с ручным душем; встраиваемая часть в пол — до стяжки	аналог		выбор заказчика	шт	1		П1**
12	Смеситель для накладной раковины однорычажный, высокий излив, с донным клапаном	аналог		выбор заказчика	шт	2		П2, П3
13	Смеситель для умывальника однорычажный, с донным клапаном	аналог		выбор заказчика	шт	1		П12
14	Душевая система скрытого монтажа с термостатом: встраиваемая часть, верхний душ, ручная лейка	аналог		выбор заказчика	шт	1		П10**; встраиваемая часть — до плитки
15	Смеситель кухонный однорычажный, высокий излив	аналог		выбор заказчика	шт	1		Кх2
16	Смеситель для биде однорычажный, с донным клапаном	аналог		выбор заказчика	шт	1		П5
17	Сифон для отдельностоящей ванны с донным клапаном и переливом, выпуск в пол Ø40/50	аналог		выбор заказчика	шт	1		П1**
18	Сифон для умывальника бутылочный Ø32/40–50, с гофрой к выпуску	аналог		выбор заказчика	шт	3		П2, П3, П12
19	Сифон для биде Ø32/40–50	аналог		выбор заказчика	шт	1		П5
20	Сифон для мойки Ø40/50	аналог		выбор заказчика	шт	1		Кх2
21	Сифон для посудомоечной машины с обратным клапаном, на выводе слива Ø40	аналог		выбор заказчика	шт	1		Кх3
22	Сифон для стиральной машины встраиваемый в стену Ø50, с обратным клапаном	аналог		выбор заказчика	шт	1		П6
23	Кран угловой ½"×½" с гибкой подводкой 40 см (умывальники, биде, мойка)	аналог		выбор заказчика	шт	10		по 2 на прибор
24	Кран шаровой угловой ½"×¾" для подключения стиральной и посудомоечной машины	аналог		выбор заказчика	шт	2		П6, Кх3

Поз.	Наименование и техническая характеристика	Тип, марка, обозначение документа	Код продукции	Поставщик	Ед. изм.	Кол.	Масса 1 ед., кг	Примечание
	Трубопроводы							
25	Труба полипропиленовая PP-R PN20 Ø20×3,4 (В1)	ГОСТ 32415-2013		выбор заказчика	м	25	0,17	15,3 + 7,0 + 10 %
26	Труба PP-R, армированная стекловолокном, PN20 Ø20×2,8 (Т3)	ГОСТ 32415-2013		выбор заказчика	м	19	0,15	13,6 + 3,7 + 10 %
27	Труба канализационная ПП Ø40 (К1)	ГОСТ 32414-2013		выбор заказчика	м	1		0,3 + 0,6 + 10 %
28	Труба канализационная ПП Ø50 (К1)	ГОСТ 32414-2013		выбор заказчика	м	16		11,5 + 2,8 + 10 %
29	Труба канализационная ПП Ø110 (К1)	ГОСТ 32414-2013		выбор заказчика	м	2,5		1,7 + 0,4 + 10 %
	Фасонные части и выводы							
30	Отвод канализационный ПП 45° Ø40	ГОСТ 32414-2013		выбор заказчика	шт	2		2 шт. на поворот
31	Отвод канализационный ПП 45° Ø50	ГОСТ 32414-2013		выбор заказчика	шт	16		2 шт. на поворот
32	Отвод канализационный ПП 45° Ø110	ГОСТ 32414-2013		выбор заказчика	шт	12		2 шт. на поворот
33	Тройник канализационный ПП 45° (врезки ветвей)	ГОСТ 32414-2013		выбор заказчика	шт	10		
34	Ревизия канализационная ПП (после поворота трассы)	ГОСТ 32414-2013		выбор заказчика	шт	8		доступ сохранить
35	Фитинги PP-R Ø20: тройники, угольники 90° (ветви и повороты В1, Т3)	ГОСТ 32415-2013		выбор заказчика	шт	44		
36	Водорозетка PP-R Ø20×½" настенная, с креплением	ГОСТ 32415-2013		выбор заказчика	шт	16		коды — лист выводов
37	Вывод в пол PP-R Ø20 под встраиваемую часть напольного смесителя (переход на ½" по паспорту смесителя)	ГОСТ 32415-2013		выбор заказчика	шт	2		П1**
	Узлы ввода, люки, короба							
38	Кран шаровой латунный Ду15 PN16 (отключение ввода)	аналог		выбор заказчика	шт	6		Ст В1-1, Ст Т3-1, Ст В1-2, Ст Т3-2, Ст В1-3, Ст Т3-3
39	Фильтр сетчатый косой Ду15	аналог		выбор заказчика	шт	6		
40	Счётчик воды крыльчатый Ду15 (ХВ, ГВ), с поверкой	аналог		выбор заказчика	шт	6		пломба УК
41	Клапан обратный Ду15	аналог		выбор заказчика	шт	6		
42	Люк ревизионный нажимной под плитку 300×400 мм	аналог		выбор заказчика	шт	3		к стоякам и арматуре
43	Звукоизоляция стояка К1 в коробе: рулонный звукоизоляционный материал ≥ 10 мм, обмотка стояка на высоту этажа	аналог		выбор заказчика	м	8,1		Ст К1-1, Ст К1-2, Ст К1-3 (кухня)
44	Короб К1 над полом: профиль ПН/ПС, ГКЛВ 12,5 мм под плитку	аналог		выбор заказчика	м	11,2		сечение — лист разводки

Примечания

1. Форма 1 ГОСТ 21.110-2013, ширины граф изменены по п. 4.1. «Аналог» — аналог по характеристикам: модели внести до черновых работ, привязки выводов сверить по паспортам.
2. Бытовая техника не входит (показана арматура подключения), мойка — в комплекте кухни (марка — модуля кухни, как у столяра). Длины труб — трасса листа разводки + подъёмы + 10 %.
3. Стояк К1 в коробе — звукоизоляция стояка в коробе без жёсткого контакта короба с трубой.
4. Расчёт систем водоснабжения и канализации, диаметры магистралей и подбор оборудования выполняет проектная организация.

Изм.	Кол.уч	Лист	№ док.	Подп.	Дата
Разраб.		Кырлан А.С.			04.11.26
Пров.					
ГИП					
Н. контр.					
Утв.					

ГД-2026-008-АИ

Квартира с кабинетом

Общая площадь 127,29* м² · * размеры со скана, не замерены (реестр — л. 6–8, К-1)

Дизайн-проект интерьера	Стадия	Лист	Листов
	РП	46	131

Спецификация сантехнического оборудования

М б/м

Кырлан Александр Сергеевич

Техническое задание на подбор светильников

ПРЕДВАРИТЕЛЬНО · не для производства работ · открыто пунктов: 13 (реестр — л. 6–8)

Параметры для подбора: светильники, ленты и блоки питания, слои света, сценарии помещений со светорегуляторами · б/м

Параметры светильников для подбора

Поз.	Марки	Наименование	Установка	Кол.	P, Вт	Σ P, Вт	Ф, лм	Тц, K	Ra	Угол, °	IP	Дим.	Слой	Группа	Пом.
1	Св1–Св8	Встраиваемый точечный	в ГКЛ, корпус ≤ 70 мм	8	12	96	1000	2700	90	—	20	—	общий	L1	1
2	Св9	Лента светодиодная 24 В	в карнизе короба, профиль с рассеивателем	13,3 м	9,6/м	127,3	900/м	2700	90	—	20	да	акцентный	L2	1
3	Св10, Св11, Св24, Св25, Св62, Св63	Настенный (бра)	на стене, H=1500	6	6	36	400	2700	90	60	20	—	рабочий	L3, L9, L21	1, 3, 6
4	Св16	Потолочный накладной	на потолке, засветка стены	1	10	10	900	3000	90	—	20	—	общий	L6	2
5	Св17–Св22, Св55–Св60	Встраиваемый точечный	в ГКЛ, корпус ≤ 70 мм	12	12	144	1050	2700	90	—	20	—	общий	L7, L19	3, 6
6	Св23	Лента светодиодная 24 В	в карнизе короба, профиль с рассеивателем	14,3 м	9,6/м	137,7	900/м	2700	90	—	20	да	акцентный	L8	3
7	Св31**, Св32**, Св33**, Св34**, Св35**, Св36**, Св37**, Св38**, Св39**, Св40**	Встраиваемый точечный	в ГКЛ, корпус ≤ 70 мм	10	12	120	1000	3000	90	—	20	да	общий	L12	4
8	Св41	Лента светодиодная 24 В	в нише уровня, профиль с рассеивателем	7,7 м	9,6/м	74,1	900/м	2700	90	—	20	да	акцентный	L13	4
9	Св42**, Св43**, Св44**	Подвесной	подвес, низ H=1450	3	9	27	800	3000	90	—	20	да	общий	L14	4
10	Св45**, Св46**, Св47**, Св48**	Встраиваемый точечный	в ГКЛ, корпус ≤ 70 мм	4	10	40	900	3000	90	—	20	—	общий	L15	4
11	Св26–Св29, Св49**, Св53, Св54, Св64**	Встраиваемый точечный	в ГКЛ, корпус ≤ 70 мм	8	7	56	600	3000	90	—	20	да	общий, рабочий	L10, L16	4, 5, 8
12	Св61	Лента светодиодная 24 В	в карнизе короба, профиль с рассеивателем	9,6 м	9,6/м	91,8	900/м	2700	90	—	20	да	акцентный	L20	6
13	Св12–Св14, Св51	Встраиваемый точечный	в ГКЛ, корпус ≤ 70 мм	4	6	24	500	3000	90	—	44	—	общий	L4, L17	7, 9
14	Св15**, Св52**	Настенный светильник над зеркалом, драйвер встроен	над зеркалом, H=2000	2	8	16	600	3000	90	—	44	—	рабочий	L5, L18	7, 9
15	Св30**	Лента светодиодная 24 В	на поверхности, профиль с рассеивателем, датчик движения	1,8 м	4,8/м	8,6	150/м	2700	90	—	20	нет	ночной	L11	8
16	Св50	Встраиваемый точечный	в ГКЛ, корпус ≤ 70 мм	1	7	7	600	3000	90	—	44	—	общий	L17	9
		Итого		**59 шт + 46,7 м**		**1015,5**									

LED-ленты, линейные светильники и блоки питания

Марка	Пом.	L, м	U, В	Вт/м	Σ P, Вт	БП	P БП, Вт	Загр., %	Питание	Доступ к БП
Св9	1	13,3	24	9,6	127,3	БП1	200	64	с двух концов	люк 300×300 в коробе потолка ПТ1
Св23	3	14,3	24	9,6	137,7	БП2	200	69	с двух концов	люк 300×300 в коробе потолка ПТ1
Св41	4	7,7	24	9,6	74,1	БП4	300	25	с двух концов	люк 300×300 в нише фигуры потолка ПТ1
Св61	6	9,6	24	9,6	91,8	БП6	200	46	с двух концов	люк 300×300 в коробе потолка ПТ1
Св30**	8	1,8	24	4,8	8,6	БП3	20	43	с одного конца	в шкафу Пх1**, верхняя полка

Сценарии (помещения со светорегуляторами)

Помещение	Сценарий	Горят группы (уровень)	Управление
4. Кухня-гостиная	Вечер	L12 споты гостиной — 30 %; L13 подсветка короба — 100 %; L14 подвесы над столом — 50 %; остальные выкл.	светорегуляторы S8, S9**, S17**
	Ужин	L13 подсветка короба — 60 %; L14 подвесы над столом — 100 %; L16 подсветка столешницы — 30 %; остальные выкл.	светорегуляторы S9**, S10**, S17**
	Кино	L13 подсветка короба — 20 %; остальные выкл.	светорегулятор S17**
	Готовка	L12 споты гостиной — 50 %; L15 споты кухни — вкл.; L16 подсветка столешницы — 100 %; остальные выкл.	светорегуляторы S8, S10**; выключатель S18**

Слои света по помещениям

Пом.	Помещение	Слои света — группы	Σ P, Вт
1	Спальня	общий — L1; рабочий — L3; акцентный — L2	235,3
2	Гардеробная-постирочная	общий — L6	10
3	Кабинет	общий — L7; рабочий — L9; акцентный — L8	221,7
4	Кухня-гостиная	общий — L12, L14, L15; рабочий — L16; акцентный — L13	275,1
5	Коридор	общий — L10	14
6	Детская	общий — L19; рабочий — L21; акцентный — L20	175,8
7	Ванная	общий — L4; рабочий — L5	26
8	Прихожая	общий — L10; ночной — L11	36,6
9	Санузел гостевой	общий — L17; рабочий — L18	21

Допущения и предложения на листе. Основа листа: размеры сняты с растрового плана заказчика с частичными размерами: рисунок не в масштабе, помещения выровнены по подписанным размерам мебели и проходов; контрольный обмер не выполнен (К-1); высота потолка 2700 мм принята: на плане заказчика её нет (К-2); толщины стен 300 / 120 мм приняты по плану заказчика, не замерены (К-1); разрешённая мощность 15 кВт принята по типовым ТУ для квартиры, ТУ заказчиком не переданы (К-4); подрайон климата не задан — принят не северный (жилые от 2,5 м) (К-6). Знак «**» — предложение проектировщика, заказчиком не утверждено (согласовать с заказчиком): S17 — свой пост группе L13: сценарии «Вечер», «Ужин», «Кино», «Готовка» включают её отдельно от L12 — на одном светорегуляторе не набрать; S9, S10 — светорегулятор добавлен разработчиком проекта; S18 — свой пост группе L15: сценарии «Вечер», «Ужин», «Готовка» включают её отдельно от L14 — на одном светорегуляторе не набрать; Св31, Св32, Св33, Св34, Св35, Св36, Св37, Св38, Св39, Св40 — ряды — по зоне гостиной (по мебели); Св42, Св43, Св44 — диммируемость добавлена разработчиком проекта под светорегуляторы S9 и S10; Св45, Св46, Св47, Св48 — ряды — по зоне кухни (по мебели); Св49, Св64 — навесных шкафов на кухне нет: рабочий свет столешницы — потолочные светильники над столешницей (ряд по середине её глубины) (линейную подсветку «под шкафами» крепить не к чему); параметры — для подбора; диммируемость добавлена разработчиком проекта под светорегуляторы S9 и S10; Св15, Св52 — свет у зеркала — над зеркалом у умывальника по его оси (свет на лицо, а не над сантехникой); Св30 — открытая лента в накладном профиле вместо «в коробе»: короба в потолке нет — подвесной потолок помещения без короба и ниши LED; ИЗ-1: Пх1 — фасад купе по кадру визуализации прихожей: МДФ 10 мм, эмаль матовая, латунный профиль, зеркальные арочные вставки (поле 100 мм). См. лист открытых вопросов (лист 6, записи К-1, К-2, К-4, К-6; лист 7, запись ИЗ-1).

Примечания

1. Позиции и марки Св — те же, что на плане освещения (лист 26) и в ведомости светильников (лист 28); группы L — по плану выключателей (лист 27).
2. Модели светильников не выбраны: лист — техническое задание на подбор. Модель по строке таблицы: поток, Тц, Ra, угол, IP и регулировка яркости не хуже указанных, мощность не больше; встраиваемые — под глубину короба (графа «Установка»). IP 20 — сухие помещения. После выбора моделей (артикул, производитель) лист выпускается как «Спецификация светильников».
3. Длина LED-ленты в карнизе и нише уровня — по линиям карниза и ниши плана потолков (лист 48); Σ P = Вт/м × длина. Блок питания загружен не больше чем на 80 %; лента 24 В длиннее 10 м питается с двух концов; доступ к блоку питания — люк ревизии 300×300 мм или место, указанное в таблице.
4. Сценарии: % — яркость группы на светорегуляторе; «вкл.» — группа на обычной клавише; группы, не названные в строке, выключены. Светильники и блоки питания групп на светорегуляторе — с регулировкой яркости. Клавиши и светорегуляторы — лист 27.
5. В пом. 1, 3, 6 свет включается клавишами групп — лист 27.
6. Мощность и поток в таблице — требования к подбору (поток не меньше, мощность не больше указанных); после выбора модели — по её паспорту, Σ P — установленная мощность освещения. Оценка освещённости — на плане освещения; это не светотехнический расчёт.

Изм.	Кол.уч	Лист	№ док.	Подп.	Дата	ГД-2026-008-АИ		
						Квартира с кабинетом		
						Общая площадь 127,29* м² · * размеры со скана, не замерены (реестр — л. 6–8, К-1)		
Разраб.		Кырлан А.С.			04.11.26	Дизайн-проект интерьера	Стадия: РП	Лист: 47 / Листов: 131
Пров.								
ГИП								
Н. контр.						Техническое задание на подбор светильников	Кырлан Александр Сергеевич	
Утв.						М б/м		

выпуск 04.11.2026 № 4177cbe7a3 · стр. 52 из 166

06


Потолки и ГКЛ-конструкции

Кырлан Александр Сергеевич

выпуск 04.11.2026 № 417/cbe7a3 . стр. 53 из 166

План потолков

Уровни и марки потолков, короба с подсветкой, ниши под шторы, люки, вырезы · отметки низа от ±0,000 чистого пола · размеры в мм

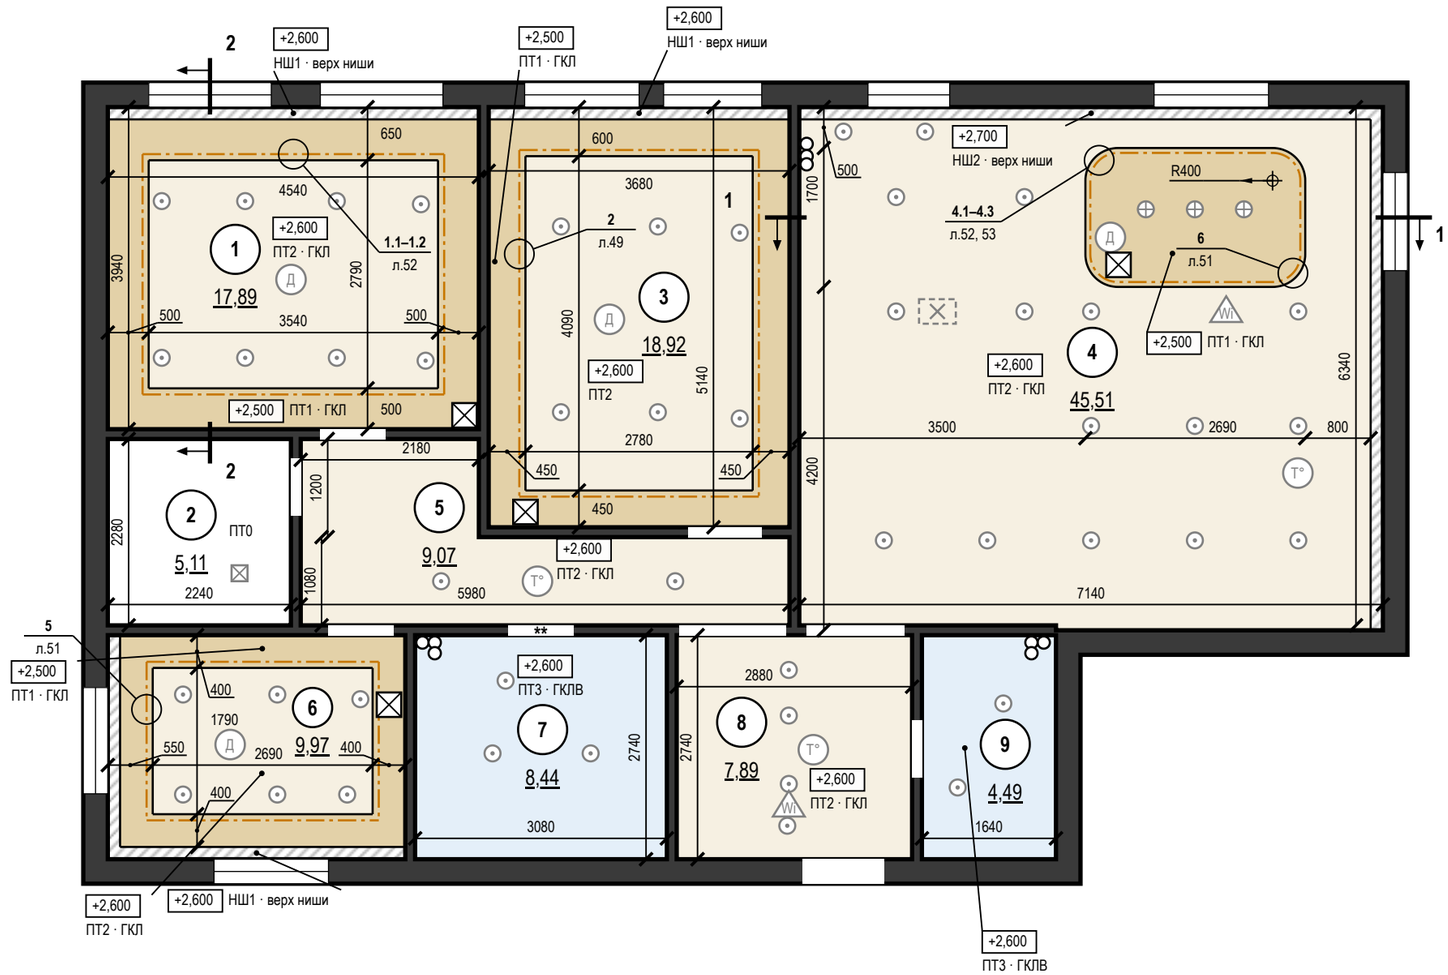

Ведомость потолков

Пом.	Марка	Конструкция	Низ / верх ниши	S, м²	Q
1	ПТ1	ГКЛ П113, короб LED	+2,500	7,33	Q3
1	ПТ2	ГКЛ П113	+2,600	9,88	Q3
1	НШ1	ниша под шторы 150×100	+2,600	0,68	
2	ПТ0	Существующий потолок, окраска	+2,700	5,11	
3	ПТ1	ГКЛ П113, короб LED	+2,500	7,00	Q3
3	ПТ2	ГКЛ П113	+2,600	11,37	Q3
3	НШ1	ниша под шторы 150×100	+2,600	0,55	
4	ПТ1	ГКЛ П113, остров + LED	+2,500	4,43	Q3
4	ПТ2	ГКЛ П113	+2,600	39,07	Q3
4	НШ2	ниша под шторы 150×100	+2,700	2,01	
5	ПТ2	ГКЛ П113	+2,600	9,07	Q3
6	ПТ1	ГКЛ П113, короб LED	+2,500	4,22	Q3
6	ПТ2	ГКЛ П113	+2,600	4,81	Q3
6	НШ1	ниша под шторы 150×100	+2,600	0,94	
7	ПТ3	ГКЛВ П113	+2,600	8,44	Q3
8	ПТ2	ГКЛ П113	+2,600	7,89	Q3
9	ПТ3	ГКЛВ П113	+2,600	4,49	Q3
		Итого		**127,29**	

Условные обозначения

- ПТ1 — ГКЛ по каркасу П113, низ +2,500, пояс-короб с карнизом LED
- ПТ2 — ГКЛ по каркасу П113, низ +2,600
- ПТ3 — ГКЛВ по каркасу П113, низ +2,600
- ПТ0 — существующий потолок, окраска, без подвесного потолка, низ +2,700
- НШ1 — ниша под шторы 150×100, верх +2,600
- НШ2 — ниша под шторы 150×100, верх +2,700
- граница уровней потолка (перепад)
- LED-лента в нише подсветки (карниз короба, ниша фигуры)
- стояк: К1 — канализация, В1 — ХВС, Т3 — ГВС
- люк ревизии в потолке 300×300 мм (доступ к БП LED)
- светильник встраиваемый — подложка с плана освещения
- светильник накладной — подложка с плана освещения
- светильник подвесной — подложка с плана освещения
- Д — извещатель дымовой на потолке — подложка
- Т° — извещатель тепловой на потолке — подложка
- Wi — точка доступа Wi-Fi на потолке — подложка

Условные обозначения (продолжение)

- вытяжка островная над островом: закладная под подвес к плите (крест) — по паспорту модели
- линия разреза у стен помещения, стрелка — направление взгляда
- место узла и сечений М 1:10: номер узла или сечений на полке, под полкой — лист
- +2,600 — отметка низа потолка, м (у ниши под шторы — верх ниши); под ней марка потолка
- 1 — номер помещения, площадь м²

Ведомость вырезов и закладных в потолке

Марка	Устройство	Кол.	Пом.
	Светильник встраиваемый (марки — план освещения)	47	1, 3, 4, 5, 6, 7, 8, 9
	Светильник накладной (марки — план освещения)	1	2
	Светильник подвесной (марки — план освещения)	3	4
ИП1, ИП2, ИП4, ИП7	Извещатель дымовой	4	1, 3, 4, 6
ИП5, ИП6, ИП3	Извещатель тепловой	3	4, 5, 8
АР2**, АР1**	Точка доступа Wi-Fi, PoE	2	4, 8
Кх6**	Вытяжка островная: закладная под подвес к плите, проход штанги и вывод питания через ГКЛ по паспорту модели	1	1
	Люк ревизии 300×300	4	1, 3, 4, 6

Примечания

1. За отметку ±0,000 принят уровень чистого пола сухих помещений (готовое покрытие), а не существующего пола; пол пом. 7, 9 — −0,015; верх плиты перекрытия −0,064 — расчётный по пирогу пола, не замерен; существующий пол снимается до плиты, его отметка не замерена. Отметки в прямоугольниках — низ потолка; низ перекрытия +2,700. Марка потолка — одна конструкция и отметка на весь альбом.
2. Размеры помещений в свету (ширина × длина, мм), не поместившиеся на плане: пом. 4 — 7140 × 6340, 4000 × 60; пом. 6 — 3640 × 2740; пом. 9 — 1640 × 2740.
3. Потолки ГКЛ — каркасная система П113: подвесы через 1000 (с запасом: СП 163, табл. 14 — до 1100 при 0,15 кН/м²), несущие профили через 500, основные через 1200 мм; листы — поперёк несущих профилей. В помещениях 7, 9 — ГКЛВ на оцинкованном каркасе.
4. Нижний уровень — пояс-короб по периметру шириной 500, 450, 400 мм, верхний — поле внутри пояса: пом. 1, 3, 6.
5. LED-лента в алюминиевом профиле посередине карниза короба шириной 500, 450, 400 мм (узел 1 — пом. 1, лист 49; узел 2 — пом. 3, лист 49; узел 5 — пом. 6, лист 51); длина по плану: пом. 1 — 13,3 м (в плане освещения 13,3); пом. 3 — 14,3 м (в плане освещения 14,3); пом. 6 — 9,6 м (в плане освещения 9,6).
6. Ниши под шторы 150×100 мм — на всю длину стены с окном; карниз — на закладной до обшивки (узел 4 — пом. 1, 3, 6, лист 50; узел 3 — пом. 4, лист 49).
7. Светильники и потолочные устройства — подложка с планов освещения, слаботочных систем и вентиляции (положение — по ним); вырезы и закладные — по ведомости на листе, до обшивки; отверстия не совмещать с профилями, глубина корпуса светильника до 70 мм.
8. Разрезы 1–1, 2–2 — на листе 49; высоты мебели и дверных блоков сверены с низом потолка в разрезах; гибка бортов фигур и ленты ниш — там же; размеры фигурных уровней — фрагмент 1 (лист 50).
9. Узлы по выноскам на плане: узлы 1, 2, 3 — лист 49; узел 4 — лист 50; узлы 5, 6 — лист 51; сечения М 1:10 по помещениям — листы 52, 53.
10. Шпаклевание ГКЛ и условия приёмки — Q3: рассеянный дневной свет, осмотр с 2 м; боковой свет не оценивается.
11. Люки ревизии 300×300 мм — по центру блоков питания LED (БП1, БП2, БП4, БП6; координаты — план освещения).
12. Сечения потолков М 1:10: пом. 3 — 3.1, 3.2 (лист 52); пом. 6 — 6.1, 6.2 (лист 53).

1000 мм · печать 1:1

Допущения и предложения на листе. Знак «**» предложено (согласовать). См. лист открытых вопросов (листы 6–8).

ПРЕДВАРИТЕЛЬНО · не для производства работ · открыто пунктов: 13 (реестр — л. 6–8)

ГД-2026-008-АИ

Квартира с кабинетом

Общая площадь 127,29* м² · * размеры со скана, не замерены (реестр — л. 6–8, К-1)

Изм.	Кол.уч	Лист	№ док.	Подп.	Дата
Разраб.		Кырлан А.С.			04.11.26
Пров.					
ГИП					
Н. контр.					
Утв.					

Стадия	Лист	Листов
РП	48	131

Дизайн-проект интерьера
1, 3, 4, 6

План потолков

М 1:75

Кырлан Александр Сергеевич

выпуск 04.11.2026 · 4177cbe7a3 · стр. 54 из 166


Разрезы и узлы потолков

Разрезы по потолкам с отметками уровней · узлы коробов и ниш · размеры в мм

ПРЕДВАРИТЕЛЬНО · не для производства работ · открыто пунктов: 13 (реестр — л. 6–8)


Разрез 1–1 (М 1:40)

Пом. 4 Кухня-гостиная; линия разреза — план потолков, лист 48

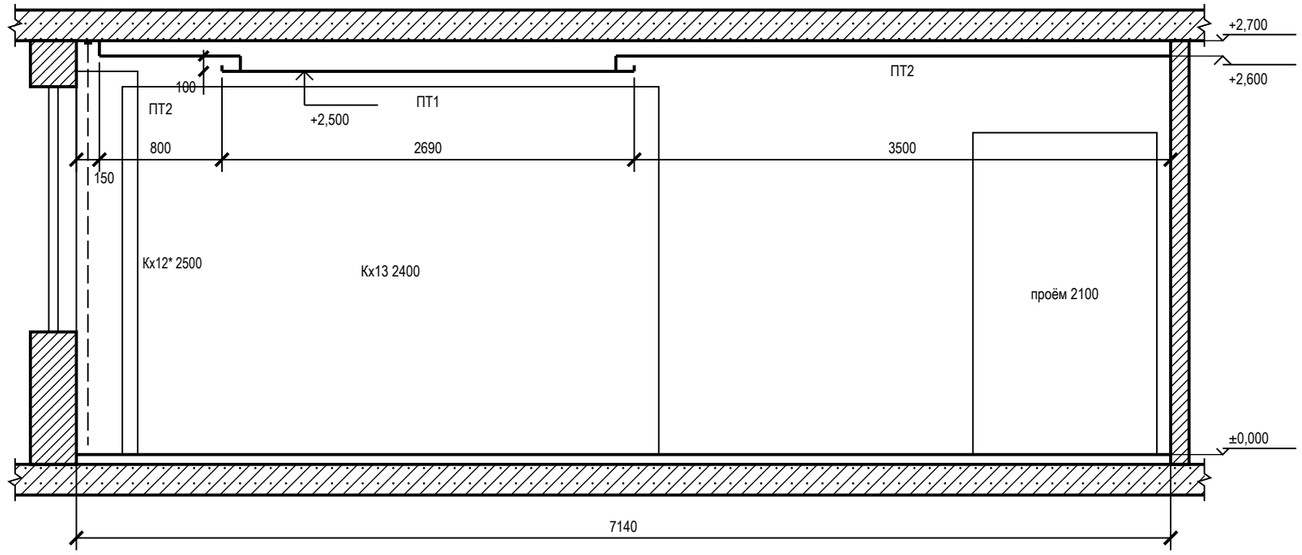


Разрез 2–2 (М 1:40)

Пом. 1 Спальня; линия разреза — план потолков, лист 48

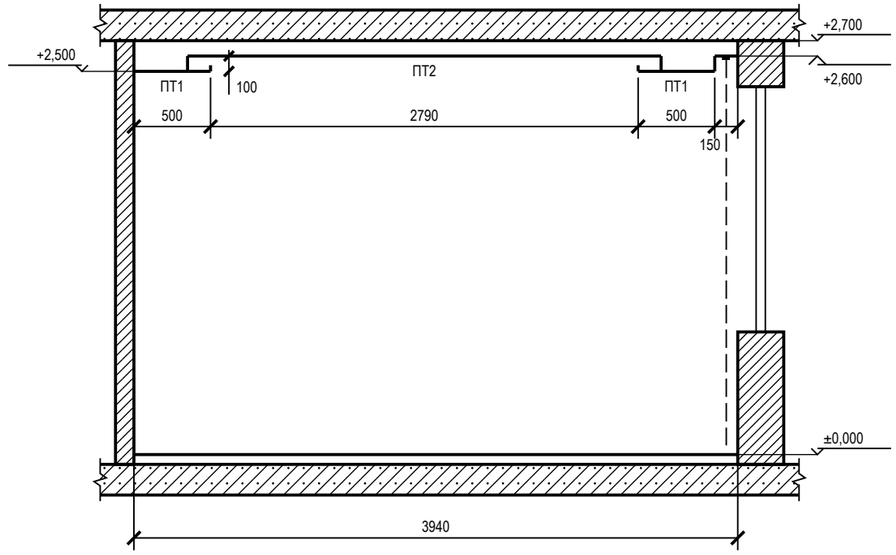

1 Короб с LED-подсветкой (М 1:10)


Пом. 1; карниз 150×100, щель под свет 60 мм

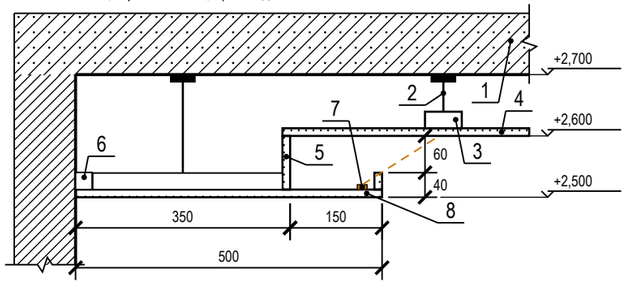

1 — плита перекрытия
2 — подвес прямой, шаг 1000 мм
3 — ПП 60×27: несущие через 500, основные через 1200 мм
4 — ГКЛ 12,5 по П113 — верхний уровень
5 — задняя стенка и бортик карниза — ГКЛ 12,5
6 — ПН 28×27 по периметру, к стене через 500 мм
7 — LED-лента в алюминиевом профиле
8 — низ короба — ГКЛ 12,5 по ПП 60×27

2 Короб с LED-подсветкой (М 1:10)

Пом. 3; карниз 150×100, щель под свет 60 мм

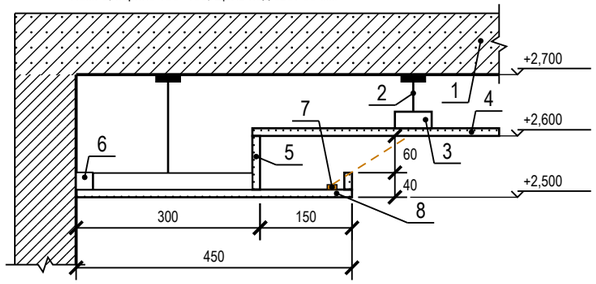

1 — плита перекрытия
2 — подвес прямой, шаг 1000 мм
3 — ПП 60×27: несущие через 500, основные через 1200 мм
4 — ГКЛ 12,5 по П113 — верхний уровень
5 — задняя стенка и бортик карниза — ГКЛ 12,5
6 — ПН 28×27 по периметру, к стене через 500 мм
7 — LED-лента в алюминиевом профиле
8 — низ короба — ГКЛ 12,5 по ПП 60×27


Условные обозначения

- плита перекрытия в сечении
- стена в сечении
- потолок ГКЛ в сечении; под линией — марка потолка (план потолков)
- мебель и дверные проёмы за секущей плоскостью; число — марка и верх от чистого пола, мм
- портьера в нише под шторы

Допущения и предложения на листе. Основа листа: размеры сняты с растрового плана заказчика с частичными размерами: рисунок не в масштабе, помещения выровнены по подписанным размерам мебели и проходов; контрольный обмер не выполнен (К-1); высота потолка 2700 мм принята: на плане заказчика её нет (К-2); толщины стен 300 / 120 мм приняты по плану заказчика, не замерены (К-1); разрешённая мощность 15 кВт принята по типовым ТУ для квартиры, ТУ заказчиком не переданы (К-4); подрайон климата не задан — принят не северный (жилые от 2,5 м) (К-6). Знак «*» — принято, не замерено (замерить): ИЗ-5, ИЗ-9, К-20: Кх12. См. лист открытых вопросов (лист 6, записи К-1, К-2, К-4, К-6; лист 7, запись К-20; лист 8, записи ИЗ-5, ИЗ-9).

3 Ниша под шторы (М 1:10)

Пом. 4; без подсветки; закладные под карниз — до обшивки

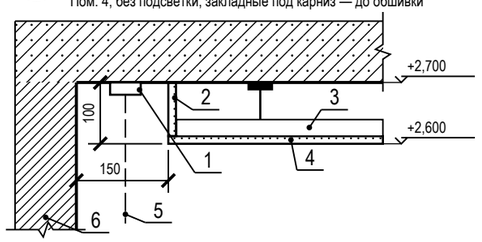

1 — карниз (шина), высота с верхом портьеры 80 мм
2 — стенка ниши — ГКЛ 12,5
3 — ПП 60×27 — каркас короба
4 — низ короба нижнего уровня — ГКЛ 12,5
5 — портьера
6 — стена с окном

Примечания

1. Разрезы — по линиям 1–1, 2–2 на плане потолков (лист 48). Отметки — от ±0,000 чистого пола, м; размеры — мм.
2. Высоты мебели и дверных блоков за секущей плоскостью сверены с низом потолка над ними: верх ниже низа короба и поля.
3. ГКЛ 12,5 мм по каркасу П113; перепад уровней и бортик карниза — ГКЛ по ПП 60×27 (узел 1 — на этом листе; узел 2 — на этом листе; узел 5 — лист 51). Ниша под шторы — на всю длину стены с окном, карниз на закладной до обшивки (узел 4 — лист 50; узел 3 — на этом листе).
4. Толщины плит перекрытия и пирога пола показаны условно.
5. Сечения потолков по помещениям М 1:10 (отметки помещения, профили, подвесы, крепёж, изделия) — листы 52–53.
6. Ведомость объёмов потолков (лист ГКЛ, профиль, подвесы, лента, блоки питания, люки) — на листе 50.
7. Фрагмент 1 — помещение с фигурными уровнями (размеры фигур, радиусы, отметки) — на листе 50.

1000 мм · печать 1:1

Изм.	Кол.уч	Лист	№ док.	Подп.	Дата
Разраб.		Кырлан А.С.			04.11.26
Пров.					
ГИП					
Н. контр.					
Утв.					

ГД-2026-008-АИ

Квартира с кабинетом

Общая площадь 127,29* м² · * размеры со скана, не замерены (реестр — л. 6–8, К-1)

Дизайн-проект интерьера

Стадия	Лист	Листов
РП	49	131

Разрезы и узлы потолков

М 1:40; 1:10

Кырлан Александр Сергеевич


выпуск 04.11.2026 № 4177cbe7a3 · стр. 55 из 166

Разрезы и узлы потолков (продолжение)

Узлы коробов и ниш · фрагменты фигурных уровней · ведомость объёмов · размеры в мм

Фрагмент 1. Пом. 4 Кухня-гостиная — уровни потолка (М 1:50)

Цепочки — от чистых граней стен; отметки — низ уровня от ±0,000

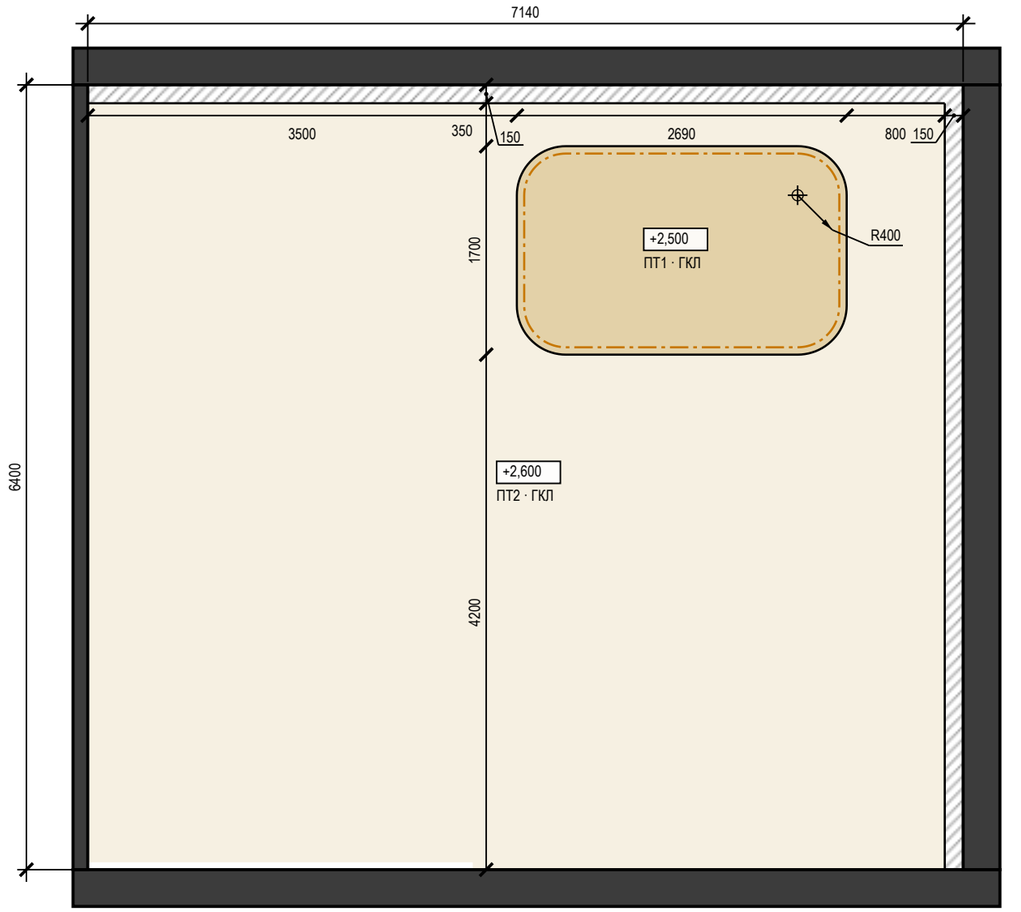

ПТ1 — низ +2,500 · ПТ2 — низ +2,600 · LED-лента в нише подсветки (карниз короба, ниша фигуры) · ниша под шторы

Ведомость объёмов потолков

Позиция	Ед.	Кол.	Пом.
Лист ГКЛ 12,5	м²	124,34	1, 3, 4, 5, 6, 8
Лист ГКЛВ 12,5	м²	12,93	7, 9
Лист ГКЛ арочный 6,5	м²	0,70	4
Борта и карнизы (входят в площади листов выше)	м²	15,46	1, 3, 4, 6
Профиль ПП 60×27	м	364,38	1, 3, 4, 5, 6, 7, 8, 9
Профиль ПН 28×27	м	309,84	1, 3, 4, 5, 6, 7, 8, 9
Подвес прямой	шт.	141	1, 3, 4, 5, 6, 7, 8, 9
Анкер-клин к плите	шт.	141	1, 3, 4, 5, 6, 7, 8, 9
Шуруп TN 3,5×25	шт.	3165	1, 3, 4, 5, 6, 7, 8, 9
Лента армирующая для швов	м	165,14	1, 3, 4, 5, 6, 7, 8, 9
Шпаклёвка для швов	кг	55,05	1, 3, 4, 5, 6, 7, 8, 9
Грунтовка (швы)	л	13,76	1, 3, 4, 5, 6, 7, 8, 9
Лента разделительная по периметру	м	122,60	1, 3, 4, 5, 6, 7, 8, 9
Сплошная шпаклёвка и окраска (площадь развёртки)	м²	137,62	1, 3, 4, 5, 6, 7, 8, 9
Лента LED	м	44,88	1, 3, 4, 6
Требуемая мощность блоков питания	Вт	560	1, 3, 4, 6
Установленная мощность блоков питания	Вт	900	1, 3, 4, 6
Блок питания LED	шт.	4	1, 3, 4, 6
Люк ревизии	шт.	4	1, 3, 4, 6


Допущения и предложения на листе

Основа листа: размеры сняты с растрового плана заказчика с частичными размерами: рисунок не в масштабе, помещения выровнены по подписанным размерам мебели и проходов; контрольный обмер не выполнен (К-1); высота потолка 2700 мм принята: на плане заказчика её нет (К-2); толщины стен 300 / 120 мм приняты по плану заказчика, не замерены (К-1); разрешённая мощность 15 кВт принята по типовым ТУ для квартиры, ТУ заказчиком не переданы (К-4); подрайон климата не задан — принят не северный (жилые от 2,5 м) (К-6).

См. лист открытых вопросов (лист 6, записи К-1, К-2, К-4, К-6).

4 Ниша под шторы (М 1:10)

Пом. 1, 3, 6; без подсветки; закладные под карниз — до обшивки

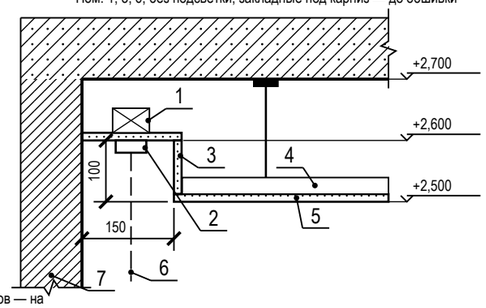

1 — закладная под карниз — брус 40×50
2 — карниз (шина), высота с верхом портьеры 80 мм
3 — стенка и потолок ниши — ГКЛ 12,5
4 — ПП 60×27 — каркас короба
5 — низ короба нижнего уровня — ГКЛ 12,5
6 — портьера
7 — стена с окном

Примечания

1. ГКЛ 12,5 мм по каркасу П113; узлы коробов и ниш под шторы: узел 1 — лист 49; узел 2 — лист 49; узел 5 — лист 51; узел 4 — на этом листе; узел 3 — лист 49; условные обозначения разрезов — на листе 49.
2. Фрагмент 1 (план потолков — лист 48) — фигурные уровни потолка крупно: привязки краёв и центров фигур к чистым граням стен, радиусы (R) с центрами, хорда и стрелка дуги, отметки низа каждого уровня; цвета уровней — как на плане потолков.
3. Фигурные уровни: борт — ГКЛ по ПН с надрезами (на дуге шаг стоек борта 300 мм при R до 2500, 400 — до 5000) или по гнутому заводскому профилю (СП 163, 6.3.3); гибка: остров пом. 4 R400 — ГКЛ 6,5 мокрой гибкой (СП 163, табл. 9). Лента в нише фигуры по оси: остров пом. 4 — 7,7 м; узел ниши LED фигуры: узел 6 — лист 51 — пом. 4.
4. Ведомость объёмов — по геометрии плана потолков: Лист ГКЛ 12,5 — плоскости уровней + борта (без арочных участков); Лист ГКЛВ 12,5 — плоскости уровней + борта; Лист ГКЛ арочный 6,5 — кривая борта × высота борта и стенки ниши × 2 слоя (R400 мокрая гибка); Борта и карнизы — длина перепада × перепад; Профиль ПП 60×27 — S × (1/шаг несущ. + 1/шаг осн.) + стойки бортов; Профиль ПН 28×27 — периметр стен + 2 × перепады + карнизы; Подвес прямой — по раскладке: S уровня / (шаг осн. × шаг подвесов), пояс уже шага — ряд вдоль пояса, фигура — по контуру; шаг подвесов — не больше табл. 14 СП 163; Анкер-клин к плите — по одному на подвес (Knauf П113); Шуруп TN 3,5×25 — 23 шт./м² (Knauf П113, табл. 2 альбома П 11); Лента армирующая для швов — 1,2 м/м² листа (Knauf); Шпаклёвка для швов — 0,4 кг/м² листа, только швы (Knauf); Грунтовка (швы) — 0,1 л/м² листа, только швы (Knauf); Лента разделительная по периметру — периметр стен под потолком ГКЛ; Сплошная шпаклёвка и окраска (площадь развёртки) — плоскости + борта; расход — по паспорту материала (норма расхода на сплошной слой не подтверждена); Лента LED — по оси карниза и ниши фигуры (план потолков); Требуемая мощность блоков питания — Вт/м × длина × 1,3; Установленная мощность блоков питания — сумма мощностей блоков по плану освещения; Блок питания LED блоки потолочных лент по плану освещения (БП1, БП2, БП4, БП6); Люк ревизии — план потолков; без запаса на подрезку (при закупке листа: ×1,075 при S > 20 м², ×1,175 — 10–20 м², ×1,275 — < 10 м²).

1000 мм · печать 1:1

Изм.	Кол.уч	Лист	№ док.	Подп.	Дата
Разраб.		Кырлан А.С.			04.11.26
Пров.					
ГИП					
Н. контр.					
Утв.					

ГД-2026-008-АИ

Квартира с кабинетом

Общая площадь 127,29* м² · * размеры со скана, не замерены (реестр — л. 6–8, К-1)

Дизайн-проект интерьера	Стадия	Лист	Листов
	РП	50	131

Разрезы и узлы потолков (продолжение)

М 1:50; 1:10


Кырлан Александр Сергеевич

Разрезы и узлы потолков (продолжение)

Узлы коробов и ниш · размеры в мм

5 Короб с LED-подсветкой (М 1:10)


Пом. 6; карниз 150×100, щель под свет 60 мм

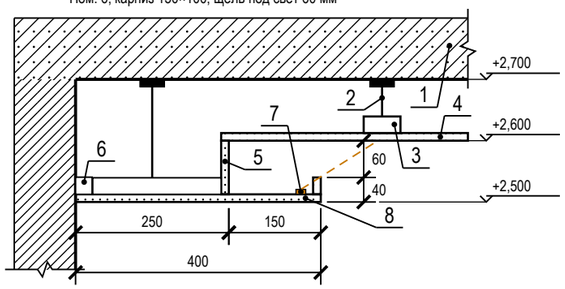

1 — плита перекрытия
2 — подвес прямой, шаг 1000 мм
3 — ПП 60×27: несущие через 500, основные через 1200 мм
4 — ГКЛ 12,5 по П113 — верхний уровень
5 — задняя стенка и бортик карниза — ГКЛ 12,5
6 — ПН 28×27 по периметру, к стене через 500 мм
7 — LED-лента в алюминиевом профиле
8 — низ короба — ГКЛ 12,5 по ПП 60×27

6 Ниша LED фигурного уровня (М 1:10)

Пом. 4; карниз 120×100, щель под свет 60 мм

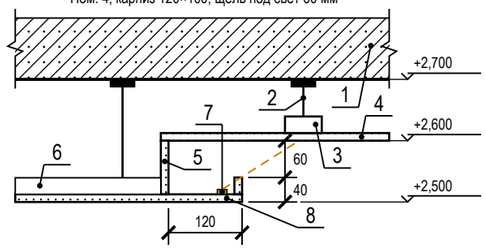

1 — плита перекрытия
2 — подвес прямой, шаг 1000 мм
3 — ПП 60×27: несущие через 500, основные через 1200 мм
4 — ГКЛ 12,5 по П113 — верхний уровень
5 — задняя стенка и бортик карниза — ГКЛ 12,5
6 — ПП 60×27 каркаса нижнего уровня, ПН по контуру фигуры (на дуге — с надрезами)
7 — LED-лента в алюминиевом профиле
8 — низ короба — ГКЛ 12,5 по ПП 60×27

Условные обозначения

— · — LED-лента в нише подсветки (карниз короба, ниша фигуры)

Примечания

1. ГКЛ 12,5 мм по каркасу П113; узлы коробов и ниш под шторы: узел 1 — лист 49; узел 2 — лист 49; узел 5 — на этом листе; узел 4 — лист 50; узел 3 — лист 49.

Допущения и предложения на листе

Основа листа: размеры сняты с растрового плана заказчика с частичными размерами: рисунок не в масштабе, помещения выровнены по подписанным размерам мебели и проходов; контрольный обмер не выполнен (К-1); высота потолка 2700 мм принята: на плане заказчика её нет (К-2); толщины стен 300 / 120 мм приняты по плану заказчика, не замерены (К-1); разрешённая мощность 15 кВт принята по типовым ТУ для квартиры, ТУ заказчиком не переданы (К-4); подрайон климата не задан — принят не северный (жилые от 2,5 м) (К-6). См. лист открытых вопросов (лист 6, записи К-1, К-2, К-4, К-6).

1000 мм · печать 1:1

Изм.	Кол.уч	Лист	№ док.	Подп.	Дата
Разраб.		Кырлан А.С.			04.11.26
Пров.					
ГИП					
Н. контр.					
Утв.					

ГД-2026-008-АИ

Квартира с кабинетом

Общая площадь 127,29* м² · * размеры со скана, не замерены (реестр — л. 6–8, К-1)

Дизайн-проект интерьера

Стадия	Лист	Листов
РП	51	131

Разрезы и узлы потолков (продолжение)

М 1:10

Кырлан Александр Сергеевич


выпуск 04.11.2026 № 4177cbe7a3 · стр. 57 из 166

Сечения потолков М 1:10

Пом. 1, 3, 4 · профили, подвесы, крепёж, изделия · размеры в мм

Сечение 1.1. Короб с LED-подсветкой (М 1:10)


Пом. 1 Спальня; карниз 150×100, щель под свет 60 мм

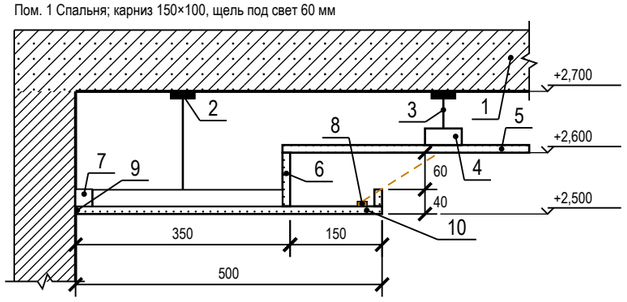

1 — плита перекрытия
2 — анкер-клин к плите — по одному на подвес
3 — подвес прямой, шаг 1000 мм
4 — ПП 60×27: несущие через 500, основные через 1200 мм; соединители одноуровневые, шурупы LN 3,5×9
5 — ГКЛ 12,5 по П113 — верхний уровень; шурупы TN 3,5×25 через 170 мм
6 — задняя стенка и бортик карниза — ГКЛ 12,5
7 — ПН 28×27 по периметру — дюбель-гвоздь через ≤ 500 мм, не менее 3 на профиль
8 — LED-лента 9,6 Вт/м, 24 В в алюминиевом профиле
9 — примыкание к стене — лента разделительная, шов зашпаклёван
10 — низ короба — ГКЛ 12,5 по ПП 60×27

Сечение 1.2. Ниша под шторы (М 1:10)


Пом. 1 Спальня; без подсветки; закладные под карниз — до обшивки

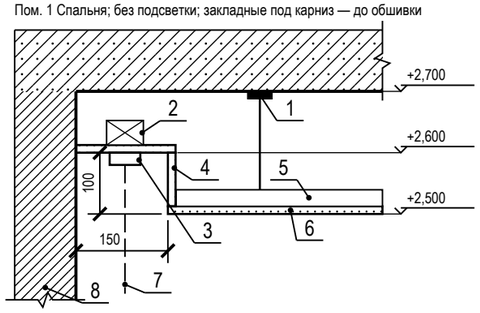

1 — анкер-клин к плите — по одному на подвес; подвес прямой, шаг 1000 мм
2 — закладная под карниз — брус 40×50
3 — карниз (шина), высота с верхом портьеры 80 мм
4 — стенка и потолок ниши — ГКЛ 12,5
5 — ПП 60×27 — каркас короба, основные через 1200 мм; соединители одноуровневые, шурупы LN 3,5×9
6 — низ короба нижнего уровня — ГКЛ 12,5; шурупы TN 3,5×25 через 170 мм
7 — портьера
8 — стена с окном

Сечение 3.1. Короб с LED-подсветкой (М 1:10)


Пом. 3 Кабинет; карниз 150×100, щель под свет 60 мм

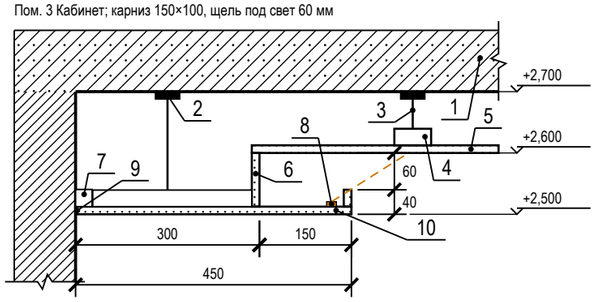

1 — плита перекрытия
2 — анкер-клин к плите — по одному на подвес
3 — подвес прямой, шаг 1000 мм
4 — ПП 60×27: несущие через 500, основные через 1200 мм; соединители одноуровневые, шурупы LN 3,5×9
5 — ГКЛ 12,5 по П113 — верхний уровень; шурупы TN 3,5×25 через 170 мм
6 — задняя стенка и бортик карниза — ГКЛ 12,5
7 — ПН 28×27 по периметру — дюбель-гвоздь через ≤ 500 мм, не менее 3 на профиль
8 — LED-лента 9,6 Вт/м, 24 В в алюминиевом профиле
9 — примыкание к стене — лента разделительная, шов зашпаклёван
10 — низ короба — ГКЛ 12,5 по ПП 60×27

Сечение 3.2. Ниша под шторы (М 1:10)


Пом. 3 Кабинет; без подсветки; закладные под карниз — до обшивки

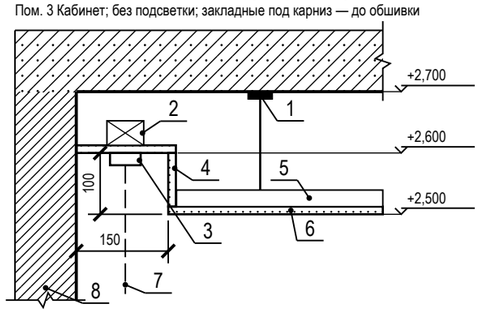

1 — анкер-клин к плите — по одному на подвес; подвес прямой, шаг 1000 мм
2 — закладная под карниз — брус 40×50
3 — карниз (шина), высота с верхом портьеры 80 мм
4 — стенка и потолок ниши — ГКЛ 12,5
5 — ПП 60×27 — каркас короба, основные через 1200 мм; соединители одноуровневые, шурупы LN 3,5×9
6 — низ короба нижнего уровня — ГКЛ 12,5; шурупы TN 3,5×25 через 170 мм
7 — портьера
8 — стена с окном

Сечение 4.1. Ниша LED фигурного уровня (М 1:10)


Пом. 4 Кухня-гостиная; карниз 120×100, щель под свет 60 мм

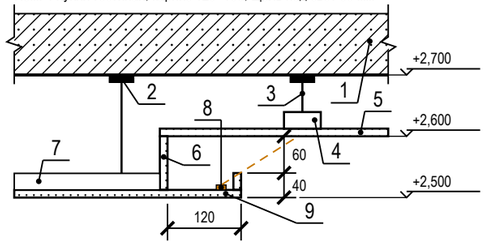

1 — плита перекрытия
2 — анкер-клин к плите — по одному на подвес
3 — подвес прямой, шаг 1000 мм
4 — ПП 60×27: несущие через 500, основные через 1200 мм; соединители одноуровневые, шурупы LN 3,5×9
5 — ГКЛ 12,5 по П113 — верхний уровень; шурупы TN 3,5×25 через 170 мм
6 — задняя стенка и бортик карниза — ГКЛ 12,5
7 — ПП 60×27 каркаса нижнего уровня, ПН по контуру фигуры (на дуге — с надрезами)
8 — LED-лента 9,6 Вт/м, 24 В в алюминиевом профиле
9 — низ короба — ГКЛ 12,5 по ПП 60×27

Сечение 4.2. Ниша под шторы (М 1:10)

Пом. 4 Кухня-гостиная; без подсветки; закладные под карниз — до обшивки

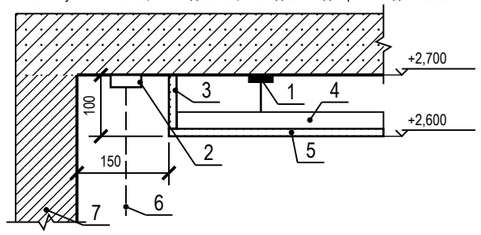

1 — анкер-клин к плите — по одному на подвес; подвес прямой, шаг 1000 мм
2 — карниз (шина), высота с верхом портьеры 80 мм
3 — стенка ниши — ГКЛ 12,5
4 — ПП 60×27 — каркас короба, основные через 1200 мм; соединители одноуровневые, шурупы LN 3,5×9
5 — низ короба нижнего уровня — ГКЛ 12,5; шурупы TN 3,5×25 через 170 мм
6 — портьера
7 — стена с окном

Условные обозначения

— · — LED-лента в нише подсветки (карниз короба, ниша фигуры)

Допущения и предложения на листе

Основа листа: размеры сняты с растрового плана заказчика с частичными размерами: рисунок не в масштабе, помещения выровнены по подписанным размерам мебели и проходов; контрольный обмер не выполнен (К-1); высота потолка 2700 мм принята: на плане заказчика её нет (К-2); толщины стен 300 / 120 мм приняты по плану заказчика, не замерены (К-1); разрешённая мощность 15 кВт принята по типовым ТУ для квартиры, ТУ заказчиком не переданы (К-4); подрайон климата не задан — принят не северный (жилые от 2,5 м) (К-6).
См. лист открытых вопросов (лист 6, записи К-1, К-2, К-4, К-6).

Примечания

1. Сечения потолков М 1:10 по помещениям с нишами LED и нишами под шторы: отметки и размеры этого помещения от ±0,000 чистого пола (м, мм). Положение — по плану потолков (лист 48): короб и ниша LED — по линиям ленты, ниша под шторы — у стены с окном; типовые узлы по группам помещений — на листе 49.
2. Крепёж: подвес прямой к плите на анкер-клине — по одному на подвес (Knauf П113); ПН к стенам — дюбель-гвоздь через ≤ 500 мм, не менее 3 на профиль (серия 1.045.9-2.08); лист 12,5 — шурупы TN 3,5×25 через 170 мм (СП 163, табл. 15); профили между собой — соединители одноуровневые, шурупы LN 3,5×9.
3. Изделие карниза, профиля LED и галтели подписано артикулом из данных; где артикул не выбран, сечение дано по габаритам из данных (ширина и глубина ниши, щель под свет), изделие подбирается по ним.

1000 мм · печать 1:1

Изм.	Кол.уч	Лист	№ док.	Подп.	Дата
Разраб.		Кырлан А.С.			04.11.26
Пров.					
ГИП					
Н. контр.					
Утв.					

ГД-2026-008-АИ

Квартира с кабинетом

Общая площадь 127,29* м² · * размеры со скана, не замерены (реестр — л. 6–8, К-1)

Дизайн-проект интерьера

Стадия	Лист	Листов
РП	52	131

Сечения потолков М 1:10

М 1:10

Кырлан Александр Сергеевич

выпуск 04.11.2026 № 4177cbe7a3 · стр. 58 из 166

Сечения потолков М 1:10

Пом. 4, 6 · профили, подвесы, крепёж, изделия · размеры в мм

Сечение 4.3. Примыкание потолка к стене (М 1:10)


Пом. 4 Кухня-гостиная; примыкание — разделительная лента



1 — плита перекрытия
2 — анкер-клин к плите — по одному на подвес
3 — подвес прямой, шаг 1000 мм
4 — ПН 28×27 по периметру — дюбель-гвоздь через ≤ 500 мм, не менее 3 на профиль
5 — ПП 60×27 несущий (вид) через 500 мм, в ПН
6 — ПП 60×27 основной (сечение) через 1200 мм; соединители одноуровневые, шурупы LN 3,5×9
7 — лента разделительная по стене, шов зашпаклёван
8 — ГКЛ 12,5 по П113; шурупы TN 3,5×25 через 170 мм

Сечение 6.1. Короб с LED-подсветкой (М 1:10)


Пом. 6 Детская; карниз 150×100, щель под свет 60 мм

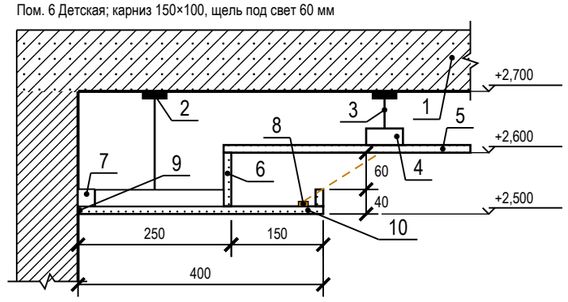

1 — плита перекрытия
2 — анкер-клин к плите — по одному на подвес
3 — подвес прямой, шаг 1000 мм
4 — ПП 60×27: несущие через 500, основные через 1200 мм; соединители одноуровневые, шурупы LN 3,5×9
5 — ГКЛ 12,5 по П113 — верхний уровень; шурупы TN 3,5×25 через 170 мм
6 — задняя стенка и бортик карниза — ГКЛ 12,5
7 — ПН 28×27 по периметру — дюбель-гвоздь через ≤ 500 мм, не менее 3 на профиль
8 — LED-лента 9,6 Вт/м, 24 В в алюминиевом профиле
9 — примыкание к стене — лента разделительная, шов зашпаклёван
10 — низ короба — ГКЛ 12,5 по ПП 60×27

Сечение 6.2. Ниша под шторы (М 1:10)

Пом. 6 Детская; без подсветки; закладные под карниз — до обшивки

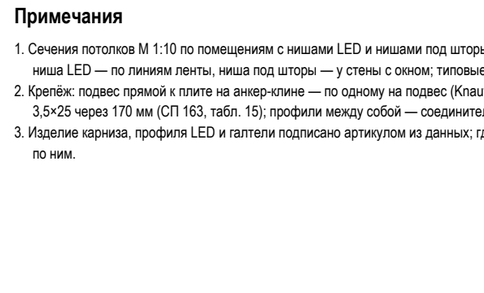

1 — анкер-клин к плите — по одному на подвес; подвес прямой, шаг 1000 мм
2 — закладная под карниз — брус 40×50
3 — карниз (шина), высота с верхом портьеры 80 мм
4 — стенка и потолок ниши — ГКЛ 12,5
5 — ПП 60×27 — каркас короба, основные через 1200 мм; соединители одноуровневые, шурупы LN 3,5×9
6 — низ короба нижнего уровня — ГКЛ 12,5; шурупы TN 3,5×25 через 170 мм
7 — портьера
8 — стена с окном

Условные обозначения

— · — LED-лента в нише подсветки (карниз короба, ниша фигуры)

Допущения и предложения на листе

Основа листа: размеры сняты с растрового плана заказчика с частичными размерами: рисунок не в масштабе, помещения выровнены по подписанным размерам мебели и проходов; контрольный обмер не выполнен (К-1); высота потолка 2700 мм принята: на плане заказчика её нет (К-2); толщины стен 300 / 120 мм приняты по плану заказчика, не замерены (К-1); разрешённая мощность 15 кВт принята по типовым ТУ для квартиры, ТУ заказчиком не переданы (К-4); подрайон климата не задан — принят не северный (жилые от 2,5 м) (К-6).
См. лист открытых вопросов (лист 6, записи К-1, К-2, К-4, К-6).

Примечания

1. Сечения потолков М 1:10 по помещениям с нишами LED и нишами под шторы: отметки и размеры этого помещения от ±0,000 чистого пола (м, мм). Положение — по плану потолков (лист 48): короб и ниша LED — по линиям ленты, ниша под шторы — у стены с окном; типовые узлы по группам помещений — на листе 49.
2. Крепёж: подвес прямой к плите на анкер-клине — по одному на подвес (Knauf П113); ПН к стенам — дюбель-гвоздь через ≤ 500 мм, не менее 3 на профиль (серия 1.045.9-2.08); лист 12,5 — шурупы TN 3,5×25 через 170 мм (СП 163, табл. 15); профили между собой — соединители одноуровневые, шурупы LN 3,5×9.
3. Изделие карниза, профиля LED и галтели подписано артикулом из данных; где артикул не выбран, сечение дано по габаритам из данных (ширина и глубина ниши, щель под свет), изделие подбирается по ним.

1000 мм · печать 1:1

Изм.	Кол.уч	Лист	№ док.	Подп.	Дата
Разраб.		Кырлан А.С.			04.11.26
Пров.					
ГИП					
Н. контр.					
Утв.					

ГД-2026-008-АИ

Квартира с кабинетом

Общая площадь 127,29* м² · * размеры со скана, не замерены (реестр — л. 6–8, К-1)

Дизайн-проект интерьера

Стадия	Лист	Листов
РП	53	131

Сечения потолков М 1:10

М 1:10

Кырлан Александр Сергеевич


выпуск 04.11.2026 № 4177cbe7a3 · стр. 59 из 166

Раскладка плитки. Планы полов


Раскладка от чистовых размеров · размеры в мм · отметки от ±0,000

ПРЕДВАРИТЕЛЬНО · не для производства работ · открыто пунктов: 13 (реестр — л. 6–8)

Фрагмент 1. Ванная (пом. 7). Пол 600×600, шов 2 мм, М 1:40

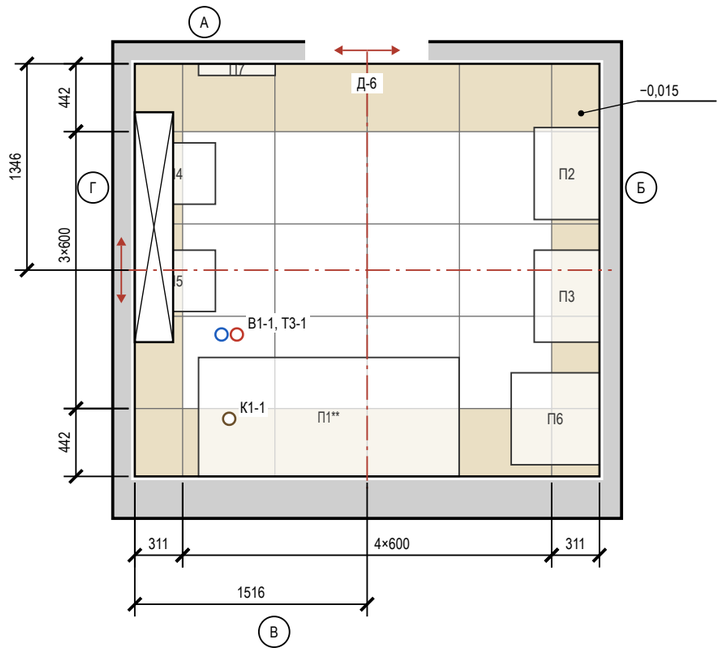

Фрагмент 2. Санузел гостевой (пом. 9). Пол 600×600, шов 2 мм, М 1:40

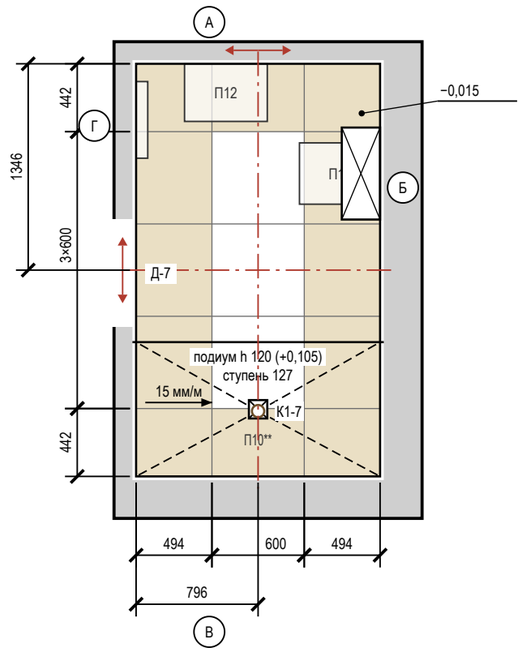

Ведомость плитки

Помещение, поверхность	Плитка, код	Формат	Шов	S, м²	Целых	Подр.	С запасом
Ванная, пол	аналог: керамогранит под травертин	600×600	2	8,44	12	18	33
Ванная, стены А–Г	A8UZ	600×1200	2	26,96	9	55	72
Ванная, короб инсталляции	A8UZ	600×1200	2	2,77	1	7	9
Санузел гостевой, пол	аналог: керамогранит под травертин	600×600	2	4,49	3	13	18
Санузел гостевой, стены А–Г	A8UZ	600×1200	2	20,72	4	42	52
Санузел гостевой, короб инсталляции	A8UZ	600×1200	2	1,47	1	3	5
Прихожая, пол	A8UZ	600×1200	2	7,89	3	12	17
Кухня-гостиная, фартук (ст. А)	аналог: керамогранит под травертин, матовый	1200×600	2	0,70	0	2	3
Итого 600×600				12,93	15	31	51
Итого 600×1200				**60,51**	**18**	**121**	**158**

Ведомость материалов

Материал	Класс, код	Норма расхода	Кол-во
Затирка	CG2WA Mapei Ultracolor Plus 132	(a+b)/ab·шов·t·1,6	5,3 кг
Затирка	CG2WA	(a+b)/ab·шов·t·1,6	0,7 кг
Клей	C2 TE S1 Ceresit CM 17	1,5 кг/м²·мм, слой 5	521 кг (21 меш.)
Клей	C2 TE S1	1,5 кг/м²·мм, слой 5	70 кг (3 меш.)
Гидроизоляция	обмазочная, 2 слоя: пол, стены по периметру и зоны замачивания	по ТУ	33,0 м²
Демпф. лента	по периметру пола из плитки		28,0 м

Условные обозначения

- плитка целая; тонкая линия — шов
- плитка с подрезкой (размер — на цепочке)
- ось старта; стрелки — направление укладки
- сантехприбор: габарит, высота по практике
- короб инсталляции: плитка пола — до короба
- трап / лоток в полу
- направление уклона К1 / пола: Ø, мм на 1 м
- край подиума; штрих — конверт к трапу
- вывод В1 (код — в ведомости привязок)
- вывод Т3 (код — в ведомости привязок)
- вывод К1 (код — в ведомости привязок)
- отметка чистого пола на полке выноски, м
- А — обозначение стены А–Г (как на развёртках)

Примечания

1. Раскладка от чистовых размеров: стены санузлов теряют 10 + 5 + 9 = 24 мм на сторону (штукатурка, клей, плитка); подрезки — чистые, без шва.
2. Старт — от центра помещения (штрихпунктир, стрелки — направление укладки); размер старта — от чистовых стен Г и А.
3. Раскладка пола «Прихожая» и фартука «Кухня-гостиная» — на листе «Раскладка плитки. Прихожая. Фартук кухни».
4. Калибр партии не задан — до укладки замерить (рабочий размер W, ГОСТ 13996-2019) и пересчитать подрезки.
5. Количество: целые по раскладке + по одной на подрезку, запас 10 %; один артикул — одна партия и тон. Исключены поддон, короб, проёмы и места за коробом; S — по чистым граням: стены нетто = зона облицовки по ведомости отделки − место за коробом инсталляции 2,52 м² (плитку за коробом не кладут), короб — отдельной строкой.
6. Клей C2 TE S1 Ceresit CM 17; C2 TE S1 (ГОСТ Р 56387-2018), затирка CG2WA Mapei Ultracolor Plus 132; CG2WA; расход — по ТУ выбранной марки.
7. Гидроизоляция: пол и стены 200 мм от ЧП; над ванной — до 2000 и 300 мм за борт (пом. 7), у душа — на всю высоту стен душевой зоны и 500 мм за край душевой зоны (пом. 9) (см. развёртки); акт скрытых работ, пролив 24 ч.
8. Подиум душа П10** (пом. 9): h 120 у трапа, решётка +0,105; верх — плиткой пола той же раскладки, уклон 15 мм/м к трапу, подрезка по линиям конверта; ступень по краю 127, грань 1592 × 127 = 0,20 м² (+1 шт. в подрезках), угол — профилем; гидроизоляция 2 сл. — по плите под подиумом, по верху и грани (узел 1 ВК); предложение, до согласования не выполнять.
9. Швы пола совмещены со швами стены А; по периметру — демпферная лента.
10. Отметка чистого пола −0,015, порог 15 мм; стык с соседним покрытием — по оси полотна двери.

Допущения и предложения на листе

Основа листа: размеры сняты с растрового плана заказчика с частичными размерами: рисунок не в масштабе, помещения выровнены по подписанным размерам мебели и проходов; контрольный обмер не выполнен (К-1); высота потолка 2700 мм принята: на плане заказчика её нет (К-2); толщины стен 300 / 120 мм приняты по плану заказчика, не замерены (К-1); разрешённая мощность 15 кВт принята по типовым ТУ для квартиры, ТУ заказчиком не переданы (К-4); подрайон климата не задан — принят не северный (жилые от 2,5 м) (К-6). Знак «**» — предложение проектировщика, заказчиком не утверждено (согласовать с заказчиком): пол пом. 7, 9 — пирог пола: стяжка 33 мм и обмазочная гидроизоляция добавлены разработчиком проекта; артикул изделия не выбран: позиция описана характеристиками («аналог по характеристикам»), артикул выбирается при закупке; К-10: П10 — Душевая зона 900 × 1640 у стены В и подиум 120 мм у трапа (ступень 127 мм) — предложение проектировщика: трап в стяжке 35 мм с облицовкой 14 мм не встаёт (монтажная высота трапа 90 до верха решётки + уклон отвода Ø50 до стояка 78 = 168 мм при врезке на уровне плиты); край подиума у проёма — вариант расстановки за автором; К-11: П1 — Стойка смесителя и выводы ванны в полу — предложение проектировщика; пирог пола — К-11.

См. лист открытых вопросов (лист 6, записи К-1, К-2, К-4, К-6, К-10, К-11).

1000 мм · печать 1:1

Изм.	Кол.уч	Лист	№ док.	Подп.	Дата
Разраб.		Кырлан А.С.			04.11.26
Пров.					
ГИП					
Н. контр.					
Утв.					

ГД-2026-008-АИ

Квартира с кабинетом

Общая площадь 127,29* м² · * размеры со скана, не замерены (реестр — л. 6–8, К-1)

Дизайн-проект интерьера

Стадия	Лист	Листов
РП	54	131

Раскладка плитки. Планы полов

М 1:40


Кырлан Александр Сергеевич

Раскладка плитки. Прихожая. Фартук кухни


Раскладка от чистовых размеров · размеры в мм · высоты фартука от чистого пола

ПРЕДВАРИТЕЛЬНО · не для производства работ · открыто пунктов: 13 (реестр — л. 6–8)

Фрагмент 1. Прихожая (пом. 8). Пол 600×1200, шов 2 мм, М 1:20

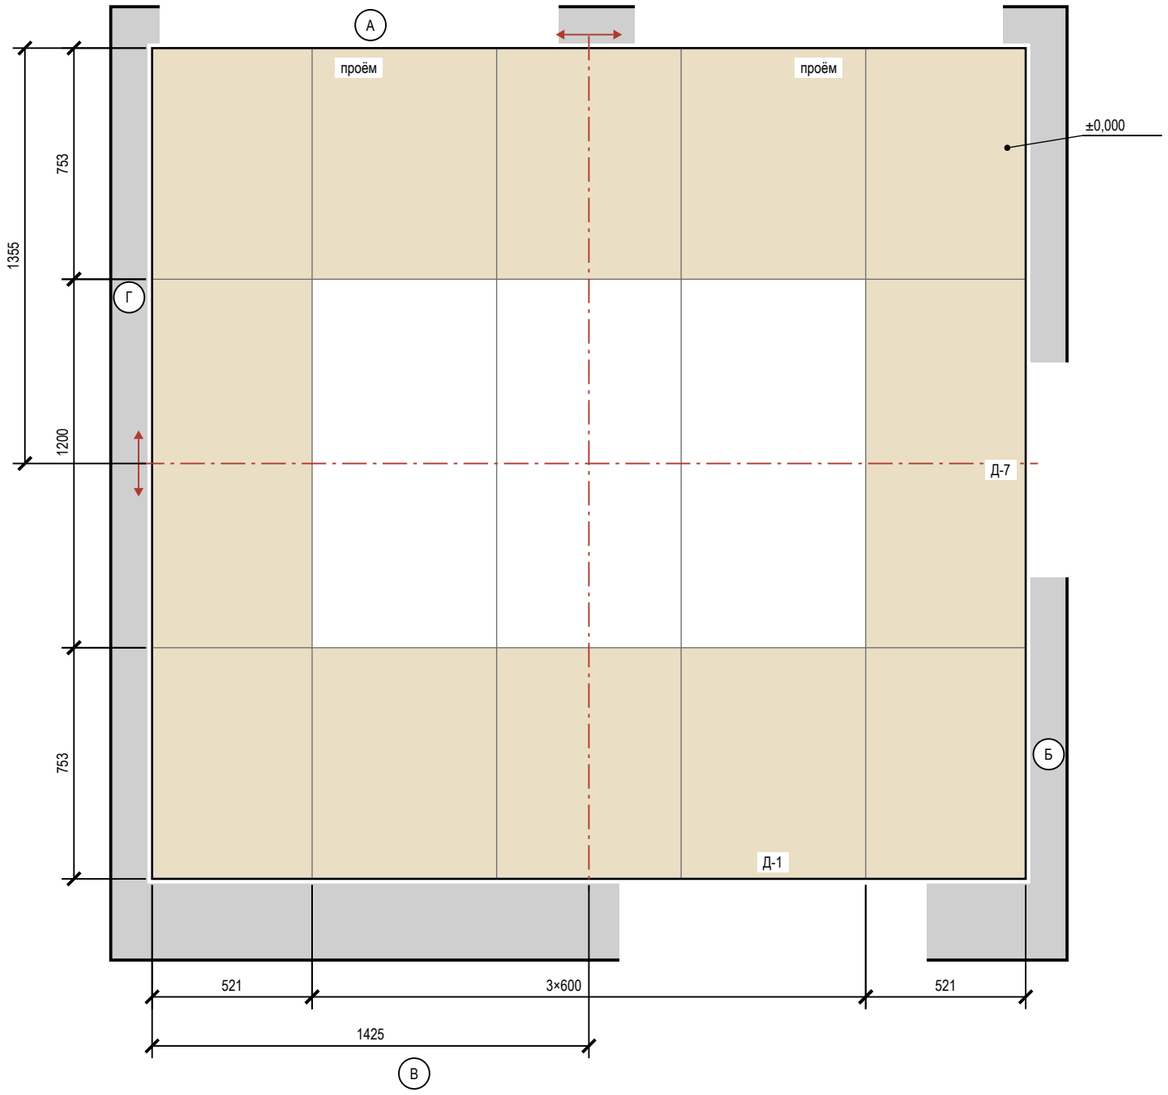

Фрагмент 2. Кухня-гостиная (пом. 4), фартук, стена А. 1200×600, шов 2 мм, М 1:20

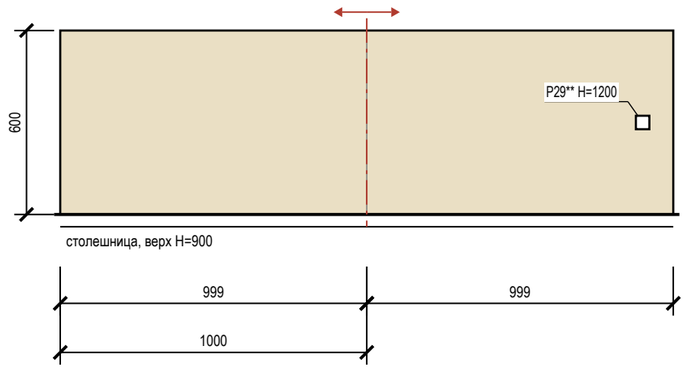

Условные обозначения

- плитка целая; тонкая линия — шов
- плитка с подрезкой (размер — на цепочке)
- ось старта; стрелки — направление укладки
- электроточка: марка и H — по листам ЭОМ
- столешница (верх)
- навесной шкаф над фартуком
- отметка чистого пола на полке выноски, м
- А — обозначение стены А–Г (как на развёртках)

Подсчёт плитки

Поверхность	Формат	S, м²	Целых	Подр.	С запасом
Прихожая, пол	600×1200	7,89	3	12	17
Кухня-гостиная, фартук (ст. А)	1200×600	0,70	0	2	3

Примечания

1. Прихожая: керамогранит 600×1200, длинная сторона — вдоль стен Б и Г, шов 2 мм, прямая раскладка от центра. Стены окрашены: раскладка от чистового контура минус штукатурка и шпаклёвка 15 мм на сторону (принято); подрезки 521 / 753 мм, срез — под плинтус.
2. Прихожая: деформационный зазор по периметру 8–10 мм под плинтусом; в проёмах — стык с соседним покрытием по оси полотна двери. Клей C2 TE S1, затирка CG2WA.
3. Фартук, Кухня-гостиная: 1200×600 горизонтально, шов 2 мм; зоны 2000 мм — 900…1500 (от столешницы до низа навесного шкафа, без шкафа — 600 мм). Старт от центра участка, подрезки 999 мм. Площадь 0,70 м² — как в ведомости отделки.
4. Фартук — после монтажа столешницы, низ на 2–3 мм выше неё, шов со столешницей — санитарный герметик; навесные шкафы — после фартука. Торцы у пенала и стены — профиль или запил 45°.
5. Клей, затирка и итог по форматам — в ведомостях листа «Раскладка плитки. Планы полов».

Допущения и предложения на листе

Основа листа: размеры сняты с растрового плана заказчика с частичными размерами: рисунок не в масштабе, помещения выровнены по подписанным размерам мебели и проходов; контрольный обмер не выполнен (К-1); высота потолка 2700 мм принята: на плане заказчика её нет (К-2); толщины стен 300 / 120 мм приняты по плану заказчика, не замерены (К-1); разрешённая мощность 15 кВт принята по типовым ТУ для квартиры, ТУ заказчиком не переданы (К-4); подрайон климата не задан — принят не северный (жилые от 2,5 м) (К-6).
Знак «**» — предложение проектировщика, заказчиком не утверждено (согласовать с заказчиком): P29 — Сдвиг под раскладку плитки фартука (стена А) на 100 мм выше — ось на шве или в центре плитки, привязка по таблице листа; плинтус пом. 4, 8, фартук пом. 4 — артикул изделия не выбран: позиция описана характеристиками («аналог по характеристикам»), артикул выбирается при закупке.
См. лист открытых вопросов (лист 6, записи К-1, К-2, К-4, К-6).

1000 мм · печать 1:1

Изм.	Кол.уч	Лист	№ док.	Подп.	Дата
Разраб.		Кырлан А.С.			04.11.26
Пров.					
ГИП					
Н. контр.					
Утв.					

ГД-2026-008-АИ

Квартира с кабинетом

Общая площадь 127,29* м² · * размеры со скана, не замерены (реестр — л. 6–8, К-1)

Дизайн-проект интерьера

Стадия	Лист	Листов
РП	55	131

Раскладка плитки. Прихожая. Фартук кухни

М 1:20


Кырлан Александр Сергеевич

выпуск 04.11.2026 № 4177cbe7a3 · стр. 61 из 166

Раскладка плитки. Ванная. Развёртки стен

ПРЕДВАРИТЕЛЬНО · не для производства работ · открыто пунктов: 13 (реестр — л. 6–8)

Пом. 7 · вид изнутри помещения · размеры в мм · высоты от чистого пола, отметки от ±0,000

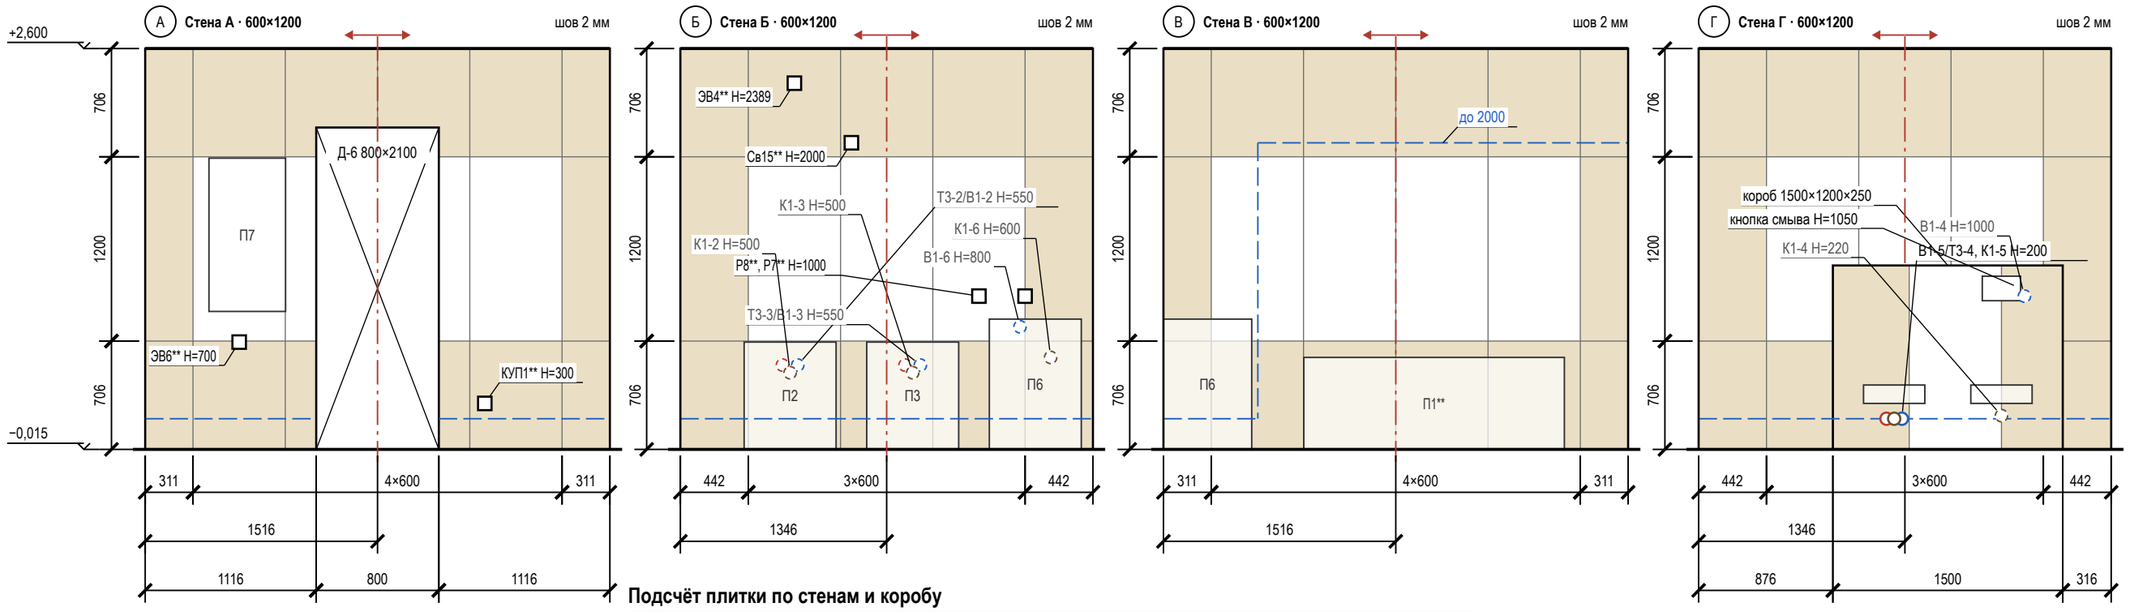

Подсчёт плитки по стенам и коробу

Поверхность	L × H, мм	S, м²	Целых	Подр.	С запасом	Подрезки: край / верх, мм
стена А	3032 × 2615	6,37	2	16	20	311 / 311; 706
стена Б	2692 × 2615	7,17	3	12	17	442 / 442; 706
стена В	3032 × 2615	8,05	4	14	20	311 / 311; 706
стена Г	2692 × 2615	5,37	0	13	15	442 / 442; 706
короб (ст. Г)	1500×1200×250	2,77	1	7	9	лицо 399 / 600 / 497; бок. 250
Итого		**29,73**	**10**	**62**	**81**	

Сдвиг точек под раскладку

Точка (ВК, ЭОМ)	Стена	Проект: от угла / Н	Под раскладку: от угла / Н	Сдвиг, мм
КУП1**	А	2216 / 300	2118 / 300	−98 на шов
Св15**	Б	1116 / 2000	1045 / 2000	−71 на шов

Условные обозначения

- плитка целая; тонкая линия — шов
- плитка с подрезкой (размер — на цепочке)
- ось старта; стрелки — направление укладки
- верх гидроизоляции: 200 от ЧП, в мокрой зоне — «до …»
- проём — не облицовывается
- сантехприбор: габарит, высота по практике
- короб инсталляции, в нём кнопка смыва 250×160
- вывод В1 (код — в ведомости привязок)
- вывод Т3 (код — в ведомости привязок)
- вывод К1 (код — в ведомости привязок)
- вывод за прибором / в коробе (не на сетке)
- электроточка: марка и Н — по листам ЭОМ
- отметка уровня, м: ±0,000 — чистый пол жилых помещений
- низ потолка; серая полоса — стена без плитки
- А — обозначение стены А–Г (как на развёртках)

Допущения и предложения на листе. Основа листа: размеры сняты с растрового плана заказчика с частичными размерами: рисунок не в масштабе, помещения выровнены по подписанным размерам мебели и проходов; контрольный обмер не выполнен (К-1); высота потолка 2700 мм принята: на плане заказчика её нет (К-2); толщины стен 300 / 120 мм приняты по плану заказчика, не замерены (К-1); разрешённая мощность 15 кВт принята по типовым ТУ для квартиры, ТУ заказчиком не переданы (К-4); подрайон климата не задан — принят не северный (жилые от 2,5 м) (К-6). Знак «**» — предложено, не утверждено (согласовать): пол пом. 7, Р7, Р8, Св15, ЭВ4, ЭВ6; ИЗ-2: КУП1; ИЗ-2, К-5: дверь пом. 7 (стена А); К-11: П1. См. лист открытых вопросов (лист 6, записи К-1, К-2, К-4–К-6, К-11; лист 7, запись ИЗ-2).

Примечания

1. Вид изнутри, стены по часовой стрелке А → Г. Высоты — от чистого пола (−0,015), отметки — от ±0,000. Раскладка от чистовых размеров (штукатурка 10 + клей 5 + плитка 9 мм), подрезки чистые; старт — от оси стены, ряды от середины (две подрезки).
2. Облицовка до потолка (+2,600).
3. Точки из таблицы сдвигов переносятся до черновой разводки (ЭОМ — по тем же числам).
4. Выводы ВК стоят по оси прибора и с прибором не двигаются — привязки по «Плану выводов сантехники» без сдвига; вне сетки (В1-5/Т3-4, К1-5) — отверстие в плитке коронкой по той же привязке, плитку не сдвигать.
5. Выводы — по «Плану выводов сантехники», электроточки — по ЭОМ, «*» — высота по практике; за приборами и в коробе (Т3-2/В1-2, К1-2, Т3-3/В1-3, К1-3, В1-6, К1-6, В1-4, К1-4) — штриховым кольцом.
6. Гидроизоляция: 200 мм от ЧП по периметру; над ванной — до 2000 и 300 мм за борт (СП 29.13330.2011, п. 7.2 — на высоту замачивания); углы — лентой; акт скрытых работ, пролив.
7. Короб 1500×1200×250: лицо 399 / 600 / 497 мм от оси кнопки смыва, боковины, полка; углы — запил 45° или профиль; за коробом плитку не кладут.

1000 мм · печать 1:1

Изм.	Кол.уч	Лист	№ док.	Подп.	Дата
Разраб.		Кырлан А.С.			04.11.26
Пров.					
ГИП					
Н. контр.					
Утв.					

ГД-2026-008-АИ

Квартира с кабинетом

Общая площадь 127,29* м² · * размеры со скана, не замерены (реестр — л. 6–8, К-1)

Дизайн-проект интерьера

Стадия	Лист	Листов
РП	56	131

Раскладка плитки. Ванная. Развёртки стен

М 1:40


Кырлан Александр Сергеевич

выпуск 04.11.2026 № 4177cbe7a3 · стр. 62 из 166

Раскладка плитки. Санузел гостевой. Развёртки стен

ПРЕДВАРИТЕЛЬНО · не для производства работ · открыто пунктов: 13 (реестр — л. 6–8)

Пом. 9 · вид изнутри помещения · размеры в мм · высоты от чистого пола, отметки от ±0,000

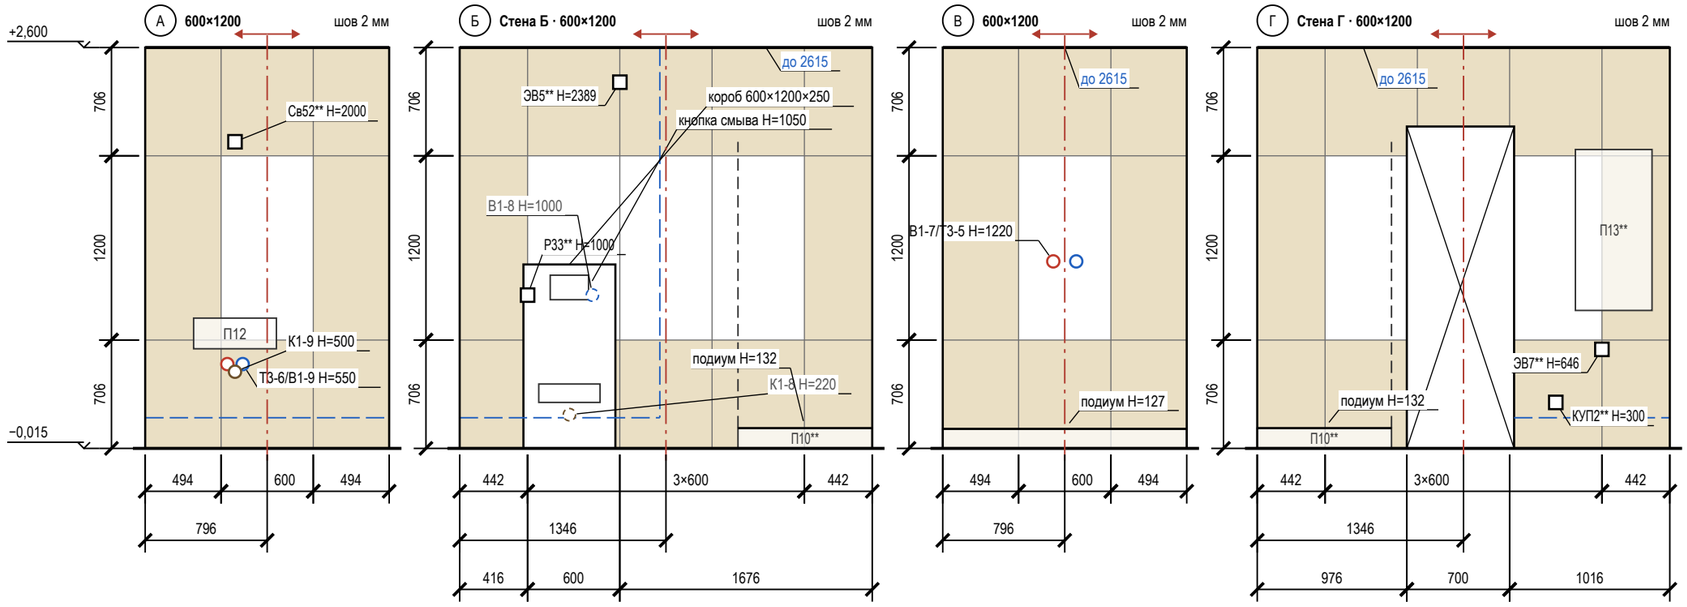

Условные обозначения

- плитка целая; тонкая линия — шов
- плитка с подрезкой (размер — на цепочке)
- ось старта; стрелки — направление укладки
- верх гидроизоляции: 200 от ЧП, в мокрой зоне — «до …»
- проём — не облицовывается
- сантехприбор: габарит, высота по практике
- граница душевой зоны (ограждение)
- короб инсталляции, в нём кнопка смыва 250×160
- вывод В1 (код — в ведомости привязок)
- вывод Т3 (код — в ведомости привязок)
- вывод К1 (код — в ведомости привязок)
- вывод за прибором / в коробе (не на сетке)
- электроточка: марка и Н — по листам ЭОМ
- отметка уровня, м: ±0,000 — чистый пол жилых помещений
- низ потолка; серая полоса — стена без плитки
- А обозначение стены А–Г (как на развёртках)

Подсчёт плитки по стенам и коробу

Поверхность	L × H, мм	S, м²	Целых	Подр.	С запасом	Подрезки: край / верх, мм
стена А	1592 × 2615	4,29	1	8	10	494 / 494; 706
стена Б	2692 × 2615	6,45	2	13	17	442 / 442; 706
короб (ст. Б)	600×1200×250	1,47	1	3	5	лицо 600; бок. 250
стена В	1592 × 2615	4,29	1	8	10	494 / 494; 706
стена Г	2692 × 2615	5,70	0	13	15	442 / 442; 706
Итого		**22,19**	**5**	**45**	**57**	

Сдвиг точек под раскладку

Точка (ВК, ЭОМ)	Стена	Проект: от угла / Н	Под раскладку: от угла / Н	Сдвиг, мм
Св52**	А	586 / 2000	495 / 2000	−91 на шов

Примечания

1. Вид изнутри, стены по часовой стрелке А → Г. Высоты — от чистого пола (−0,015), отметки — от ±0,000. Раскладка от чистовых размеров (штукатурка 10 + клей 5 + плитка 9 мм), подрезки чистые; старт — от оси стены, ряды от середины (две подрезки).
2. Облицовка до потолка (+2,600).
3. Точки из таблицы сдвигов переносятся до черновой разводки (ЭОМ — по тем же числам).
4. Выводы ВК стоят по оси прибора и с прибором не двигаются — привязки по «Плану выводов сантехники» без сдвига; вне сетки (Т3-6/В1-9, К1-9) — отверстие в плитке коронкой по той же привязке, плитку не сдвигать.
5. Выводы — по «Плану выводов сантехники», электроточки — по ЭОМ, «*» — высота по практике; за приборами и в коробе (В1-8, К1-8) — штриховым кольцом.
6. Подиум душа П10**: верх у решётки трапа +0,105 (h 120 мм), к стенам поднимается уклоном к трапу — «подиум Н=…» на развёртке — верх подиума у этой стены; облицовка стен в зоне душа — от верха подиума, грань ступени — плиткой пола. Выводы В1-7, Т3-5: Н=1220 от чистого пола помещения = 1100 от верха подиума у трапа.
7. Гидроизоляция: 200 мм от ЧП по периметру; у душа — на всю высоту стен душевой зоны и 500 мм за край душевой зоны (СП 29.13330.2011, п. 7.2 — на высоту замачивания); углы — лентой; акт скрытых работ, пролив.
8. Короб 600×1200×250: лицо 600 мм от оси кнопки смыва, боковины, полка; углы — запил 45° или профиль; за коробом плитку не кладут.

Допущения и предложения на листе. Основа листа: размеры сняты с растрового плана заказчика с частичными размерами: рисунок не в масштабе, помещения выровнены по подписанным размерам мебели и проходов; контрольный обмер не выполнен (К-1); высота потолка 2700 мм принята: на плане заказчика её нет (К-2); толщины стен 300 / 120 мм приняты по плану заказчика, не замерены (К-1); разрешённая мощность 15 кВт принята по типовым ТУ для квартиры, ТУ заказчиком не переданы (К-4); подрайон климата не задан — принят не северный (жилые от 2,5 м) (К-6). Знак «**» — предложено, не утверждено (согласовать): пол пом. 9, П13, Р33, Св52, ЭВ5, КУП2, ЭВ7; К-10: П10. См. лист открытых вопросов (лист 6, записи К-1, К-2, К-4, К-6, К-10).

1000 мм · печать 1:1

Изм.	Кол.уч	Лист	№ док.	Подп.	Дата
Разраб.		Кырлан А.С.			04.11.26
Пров.					
ГИП					
Н. контр.					
Утв.					

ГД-2026-008-АИ

Квартира с кабинетом

Общая площадь 127,29* м² · * размеры со скана, не замерены (реестр — л. 6–8, К-1)

Дизайн-проект интерьера

Стадия	Лист	Листов
РП	57	131

Раскладка плитки. Санузел гостевой. Развёртки стен

М 1:40

Кырлан Александр Сергеевич

выпуск 04.11.2026 № 4177cbe7a3 · стр. 63 из 166

07

Полы и отделка

Кырлан Александр Сергеевич

выпуск 04.11.2026 № 4177cbe7a3 · стр. 64 из 166

План полов

Покрытия, направление укладки, отметки чистого пола, стыки · размеры в мм · отметки в м

ПРЕДВАРИТЕЛЬНО · не для производства работ · открыто пунктов: 13 (реестр — л. 6–8)

Стыки покрытий в проёмах


Марка	Проём	Типы пола	Отметки ЧП	Решение
СТ1	7–5 (Д-6)	2 / 1	−0,015 / ±0,000	порог h=15 мм
СТ2	8–5	3 / 1	±0,000 / ±0,000	б/п
СТ3	8–4	3 / 1	±0,000 / ±0,000	б/п
СТ4	8–9 (Д-7)	3 / 2	±0,000 / −0,015	порог h=15 мм

Отметки по высоте




±0,000	чистый пол пом. 1–6, 8; отсчёт высот
−0,015	чистый пол пом. 7, 9, ниже на 15 мм
−0,064*	верх плиты — расчёт, не замер (задание на обмер)
сущ. пол	снимается до плиты; не замерен (задание на обмер)

Условные обозначения

- тип 1 — инженерная доска, линии — вдоль доски
- тип 2 — керамогранит 600×600, сетка — формат плитки
- тип 3 — керамогранит 600×1200, сетка — формат плитки
- 1 — номер типа пола (экспликация полов)
- схема пола, без масштаба: плита — штриховка, стяжка — точки, звукоизоляция — зигзаг, гидроизоляция — утолщённая линия с заведением на стену
- направление укладки (длинная сторона доски)
- отметка чистого пола, м
- стык в проёме: порог
- стык в проёме: без порога (б/п)
- СТ1 — марка стыка (ведомость стыков)
- стояк: К1 — канализация, В1 ХВС, Т3 — ГВС
- 1 — номер помещения, площадь м²

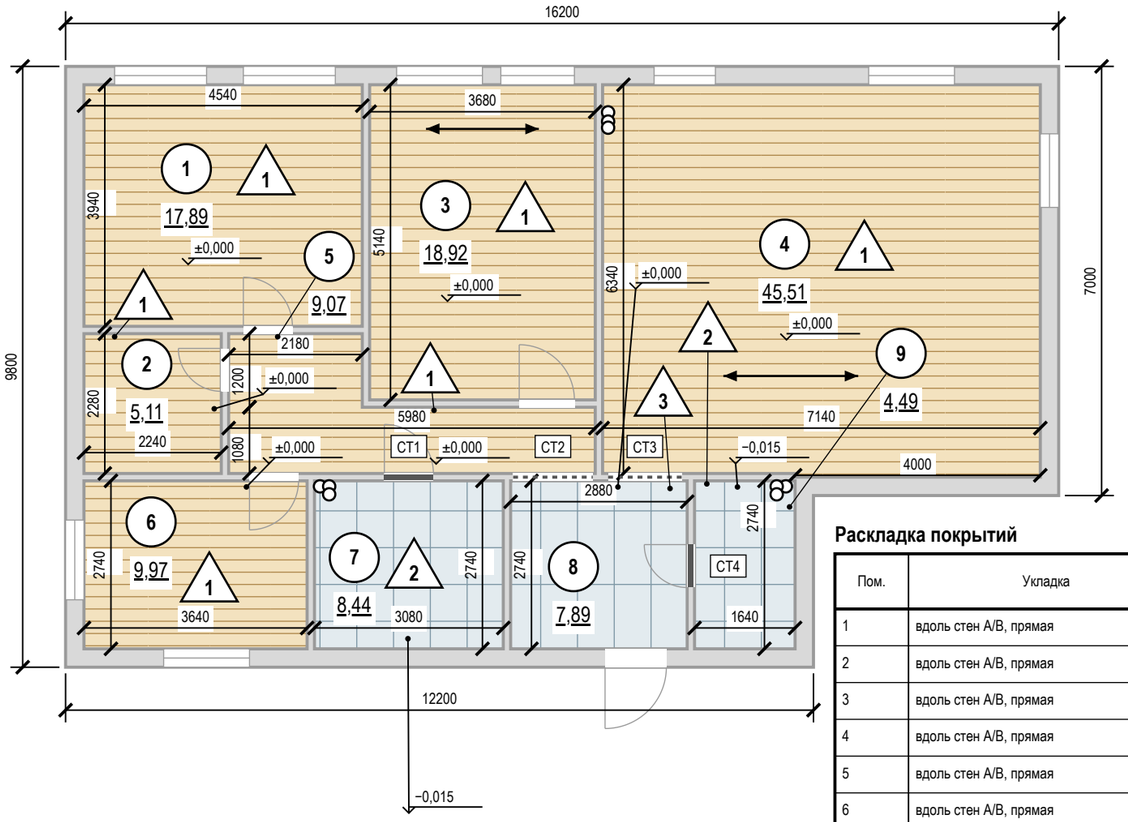

Экспликация полов

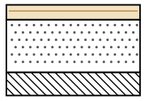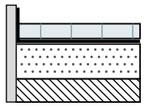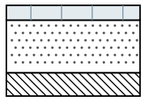Номер помещения	Тип пола	Схема пола	Данные элементов пола (наименование, толщина, основание), мм	Площадь, м²
1, 2, 3, 4, 5, 6	1		Инженерная доска на клею — 14 Стяжка ЦПС М200 — 50 Плита перекрытия Всего 64 мм; ЧП ±0,000, верх плиты −0,064	106,47
7, 9	2		Керамогранит на клею С2 TE S1 — 14 Гидроизоляция обмазочная, 2 слоя, с заведением на стены 200 мм — 2 Стяжка ЦПС М200 — 33 Плита перекрытия Всего 49 мм; ЧП −0,015, верх плиты −0,064	12,93
8	3		Керамогранит на клею С2 TE S1 — 14 Стяжка ЦПС М200 — 50 Плита перекрытия Всего 64 мм; ЧП ±0,000, верх плиты −0,064	7,89
			Итого	**127,29**

Раскладка покрытий

Пом.	Укладка	Старт (оси от чистовых стен), мм	Отступ 1-го ряда / крайние плитки, мм
1	вдоль стен A/B, прямая	от стены А, 1-й ряд вдоль неё	зазор от стены не задан
2	вдоль стен A/B, прямая	от стены А, 1-й ряд вдоль неё	зазор от стены не задан
3	вдоль стен A/B, прямая	от стены А, 1-й ряд вдоль неё	зазор от стены не задан
4	вдоль стен A/B, прямая	от стены А, 1-й ряд вдоль неё	зазор от стены не задан
5	вдоль стен A/B, прямая	от стены А, 1-й ряд вдоль неё	зазор от стены не задан
6	вдоль стен A/B, прямая	от стены В, 1-й ряд вдоль неё	зазор от стены не задан
7	прямая, сетка 600×600, шов 2	ось X 1516 от Г; ось Y 1346 от А	X 311 / 311; Y 442 / 442
8	плитка	раскладка плиточника не задана	
9	прямая, сетка 600×600, шов 2	ось X 796 от Г; ось Y 1346 от А	X 494 / 494; Y 442 / 442

Допущения и предложения на листе. Основа листа: размеры сняты с растрового плана заказчика с частичными размерами: рисунок не в масштабе, помещения выровнены по подписанным размерам мебели и проходов; контрольный обмер не выполнен (К-1); высота потолка 2700 мм принята: на плане заказчика её нет (К-2); толщины стен 300 / 120 мм приняты по плану заказчика, не замерены (К-1); разрешённая мощность 15 кВт принята по типовым ТУ для квартиры, ТУ заказчиком не переданы (К-4); подрайон климата не задан — принят не северный (жилые от 2,5 м) (К-6). Знак «**» — предложено, не утверждено (согласовать): плинтус пом. 1–5, 8, фартук пом. 4, пол пом. 7, 9; ИЗ-2, К-5: дверь пом. 7 (стена А). См. лист открытых вопросов (лист 6, записи К-1, К-2, К-4–К-6, К-10; лист 7, запись ИЗ-2).

Примечания

1. За отметку ±0,000 принят чистый пол, не существующий (блок отметок). Площади — по чистым размерам помещений, м²; размеры — в мм.
2. Стык разнотипных покрытий — по оси дверного полотна (под полотном в закрытом положении); решение стыка — по ведомости стыков.
3. Пол санузлов ниже смежных помещений на 15 мм за счёт меньшей толщины стяжки (верх плиты общий — по экспликации полов); гидроизоляция по стяжке с заведением на стены не менее 200 мм (СП 29.13330.2011, п. 7.2), до облицовки — тест проливом и акт скрытых работ.
4. Трубопроводы в конструкции пола не прокладываются: пирог пола 49–64 мм не вмещает выпуски канализации с уклоном — выпуски К1 ведутся по стенам над чистым полом в коробах (лист 37).
5. Звукоизоляционный слой под стяжкой проектом не предусмотрен (стяжка по плите): приведённый уровень ударного шума перекрытия с полом Lnw не более 60 дБ (СП 51.13330.2011, табл. 2) подтвердить по данным дома; при превышении — плавающая стяжка по звукоизоляции с демпферной лентой по контуру и у стояков, пирог пересчитать.
6. Штучные покрытия (инженерная доска): направление — по стрелке; влажность основания по СМ не более 2,0 % (по ТУ изготовителя).
7. Ровность основания — просвет под 2-метровой рейкой не более 2 мм: пом. 1, 2, 3, 4, 5, 6 (инженерная доска), пом. 7, 8, 9 (керамогранит); проверить до укладки покрытия (СП 71.13330.2017, табл. 8.5).
8. Сетка на плитке — условная, в размер формата; точка старта и раскладка — по листу раскладки плитки.
9. Узор покрытия (заливка-код типа пола) прерывается под надписями — площадями помещений и отметками чистого пола.
10. Пироги полов — по экспликации полов: слои сверху вниз, толщины в мм; гидроизоляция мокрых зон — в пироге и в ведомости отделки; схема пола — без масштаба.

1000 мм · печать 1:1

Изм.	Кол.уч	Лист	№ док.	Подп.	Дата
Разраб.		Кырлан А.С.			04.11.26
Пров.					
ГИП					
Н. контр.					
Утв.					

ГД-2026-008-АИ

Квартира с кабинетом

Общая площадь 127,29* м² · * размеры со скана, не замерены (реестр — л. 6–8, К-1)

Дизайн-проект интерьера

Стадия	Лист	Листов
РП	58	131

План полов

М 1:100

Кырлан Александр Сергеевич

выпуск 04.11.2026 № 4177cbe7a3 · стр. 65 из 166

Ведомость отделки помещений. Лист 1 из 2

Потолки, стены, низ стен, полы · площади в м², длины в м · отметки в м

Ведомость отделки помещений (форма 1 прил. А ГОСТ 21.501-2018). Лист 1 из 2

№	Наименование помещения	Потолок			Стены и перегородки			Низ стен (плинтус)			Пол		Примечание
		Вид отделки	Код цвета	S, м²	Вид отделки	Код цвета	S, м²	Вид отделки	Код цвета	L, м	Вид отделки	S, м²	
1	Спальня 17,89 м²	ГКЛ по каркасу П113, отм. +2,500; +2,600; окраска, Tikkurila Anti-Reflex 2, глубокоматовая, 2 слоя, подготовка Q3	Tikkurila V503	17,89	Окраска, Farrow & Ball Modern Emulsion, матовая, 2 слоя, подготовка Q3 Акцент — стена А: окраска, Farrow & Ball Modern Emulsion, матовая, 2 слоя, подготовка Q3	Farrow & Ball No. 15 Farrow & Ball No. 34	29,37 6,55	Плинтус МДФ h=80 мм, аналог: МДФ под покраску 80×16	Farrow & Ball No. 15	16,2	Инженерная доска, 1167-4250, 2100×127 мм, на клею; тип 1, отм. ЧП ±0,000	17,89	Н стен 2500 (до потолка); плинтус в цвет: стены
2	Гардеробная-постирочная 5,11 м²	Существующий потолок, отм. +2,700; окраска, Tikkurila Anti-Reflex 2, глубокоматовая, 2 слоя, подготовка Q3	Tikkurila V503	5,11	Окраска, Tikkurila Harmony, матовая, 2 слоя, подготовка Q3	Tikkurila V503	22,94	Плинтус МДФ h=80 мм, аналог: МДФ под покраску 80×16	Tikkurila V503	8,3	Инженерная доска, 1167-4250, 2100×127 мм, на клею; тип 1, отм. ЧП ±0,000	5,11	Н стен 2700 (до потолка); плинтус в цвет: стены
3	Кабинет 18,92 м²	ГКЛ по каркасу П113, отм. +2,500; +2,600; окраска, Tikkurila Anti-Reflex 2, глубокоматовая, 2 слоя, подготовка Q3	Tikkurila V503	18,92	Окраска, Farrow & Ball Modern Emulsion, матовая, 2 слоя, подготовка Q3 Акцент — стена А: окраска, Farrow & Ball Modern Emulsion, матовая, 2 слоя, подготовка Q3	Farrow & Ball No. 15 Farrow & Ball No. 34	33,01 5,04	Плинтус МДФ h=80 мм, аналог: МДФ под покраску 80×16	Farrow & Ball No. 15	16,7	Инженерная доска, 1167-4250, 2100×127 мм, на клею; тип 1, отм. ЧП ±0,000	18,92	Н стен 2500 (до потолка); плинтус в цвет: стены
4	Кухня-гостиная 45,51 м²	ГКЛ по каркасу П113, отм. +2,600; +2,500; окраска, Tikkurila Anti-Reflex 2, глубокоматовая, 2 слоя, подготовка Q3	Tikkurila V503	45,51	Окраска, Farrow & Ball Modern Emulsion, матовая, 2 слоя, подготовка Q3 Акцент — стена А: окраска, Farrow & Ball Modern Emulsion, матовая, 2 слоя, подготовка Q3 Фартук кухни (стена А): облицовка керамогранитом, аналог: керамогранит под травертин, матовый, 1200×600×9 мм, клей C2 TE S1, затирка CG2WA	Farrow & Ball No. 15 Farrow & Ball No. 34 по артикулу	46,70 14,92 0,70	Плинтус МДФ h=80 мм, аналог: МДФ под покраску 80×16	Farrow & Ball No. 15	25,9	Инженерная доска, 1167-4250, 2100×127 мм, на клею; тип 1, отм. ЧП ±0,000	45,51	Н стен 2600 (до потолка); матовая моющаяся, класс 1 EN 13300 — осознанно вместо полуматовой; плинтус в цвет: стены
5	Коридор 9,07 м²	ГКЛ по каркасу П113, отм. +2,600; окраска, Tikkurila Anti-Reflex 2, глубокоматовая, 2 слоя, подготовка Q3	Tikkurila V503	9,07	Окраска, Farrow & Ball Modern Emulsion, матовая, 2 слоя, подготовка Q3	Farrow & Ball No. 15	31,82	Плинтус МДФ h=80 мм, аналог: МДФ под покраску 80×16	Farrow & Ball No. 15	11,2	Инженерная доска, 1167-4250, 2100×127 мм, на клею; тип 1, отм. ЧП ±0,000	9,07	Н стен 2600 (до потолка); матовая моющаяся, класс 1 EN 13300 — осознанно вместо полуматовой; плинтус в цвет: стены
6	Детская 9,97 м²	ГКЛ по каркасу П113, отм. +2,500; +2,600; окраска, Tikkurila Anti-Reflex 2, глубокоматовая, 2 слоя, подготовка Q3	Tikkurila V503	9,97	Окраска, Farrow & Ball Modern Emulsion, матовая, 2 слоя, подготовка Q3 Акцент — стена А: окраска, Farrow & Ball Modern Emulsion, матовая, 2 слоя, подготовка Q3	Farrow & Ball No. 15 Farrow & Ball No. 34	18,48 7,42	Плинтус МДФ h=69 мм, SX165	Farrow & Ball No. 15	12,0	Инженерная доска, 1167-4250, 2100×127 мм, на клею; тип 1, отм. ЧП ±0,000	9,97	Н стен 2500 (до потолка); плинтус в цвет: стены
7	Ванная 8,44 м²	ГКЛВ по каркасу П113, отм. +2,600; окраска, Tikkurila Luja 7, матовая, 2 слоя, подготовка Q3	Tikkurila V503	8,44	Облицовка плиткой, A8UZ, 600×1200×9 мм, клей C2 TE S1, затирка CG2WA	Atlas Concorde A8UZ	28,76	нет			Аналог: керамогранит ректифицированный под травертин, матовый, 600×600×9 мм; тип 2, отм. ЧП −0,015	8,44	Н стен 2615 (до потолка); гидроизоляция обмазочная, 2 слоя, с заведением на стены 200 мм; над ванной — до 2000 и 300 мм за борт (по пирогу пола); тест проливом и акт скрытых работ
8	Прихожая 7,89 м²	ГКЛ по каркасу П113, отм. +2,600; окраска, Tikkurila Anti-Reflex 2, глубокоматовая, 2 слоя, подготовка Q3	Tikkurila V503	7,89	Окраска, Farrow & Ball Modern Emulsion, матовая, 2 слоя, подготовка Q3	Farrow & Ball No. 15	20,40	Плинтус МДФ h=80 мм, аналог: МДФ под покраску 80×16	Farrow & Ball No. 15	7,0	Керамогранит, A8UZ, 600×1200×9 мм; тип 3, отм. ЧП ±0,000	7,89	Н стен 2600 (до потолка); матовая моющаяся, класс 1 EN 13300 — осознанно вместо полуматовой; плинтус в цвет: стены

Примечания

1. Ведомость продолжена на листе 2 из 2; итоги, сводка площадей и примечания — на последнем листе ведомости.

Допущения и предложения на листе

Основа листа: размеры сняты с растрового плана заказчика с частичными размерами: рисунок не в масштабе, помещения выровнены по подписанным размерам мебели и проходов; контрольный обмер не выполнен (К-1); высота потолка 2700 мм принята: на плане заказчика её нет (К-2); толщины стен 300 / 120 мм приняты по плану заказчика, не замерены (К-1); разрешённая мощность 15 кВт принята по типовым ТУ для квартиры, ТУ заказчиком не переданы (К-4); подрайон климата не задан — принят не северный (жилые от 2,5 м) (К-6). Знак «**» — предложение проектировщика, заказчиком не утверждено (согласовать с заказчиком): плинтус пом. 1–5, 8, фартук пом. 4 — артикул изделия не выбран: позиция описана характеристиками («аналог по характеристикам»), артикул выбирается при закупке; пол пом. 7, 9 — пирог пола: стяжка 33 мм и обмазочная гидроизоляция добавлены разработчиком проекта; артикул изделия не выбран: позиция описана характеристиками («аналог по характеристикам»), артикул выбирается при закупке.

См. лист открытых вопросов (лист 6, записи К-1, К-2, К-4, К-6).

Изм.	Кол.уч	Лист	№ док.	Подп.	Дата
Разраб.		Кырлан А.С.			04.11.26
Пров.					
ГИП					
Н. контр.					
Утв.					

ГД-2026-008-АИ

Квартира с кабинетом

Общая площадь 127,29* м² · * размеры со скана, не замерены (реестр — л. 6–8, К-1)

Дизайн-проект интерьера

Стадия	Лист	Листов
РП	59	131

Ведомость отделки помещений. Лист 1 из 2

М б/м

Кырлан Александр Сергеевич

выпуск 04.11.2026 № 4177cbe7a3 · стр. 66 из 166

Ведомость отделки помещений. Лист 2 из 2

ПРЕДВАРИТЕЛЬНО · не для производства работ · открыто пунктов: 13 (реестр — л. 6–8)

Потолки, стены, низ стен, полы · площади в м², длины в м · отметки в м

Ведомость отделки помещений (форма 1 прил. А ГОСТ 21.501-2018). Лист 2 из 2

№	Наименование помещения	Потолок			Стены и перегородки			Низ стен (плинтус)			Пол		Примечание
		Вид отделки	Код цвета	S, м²	Вид отделки	Код цвета	S, м²	Вид отделки	Код цвета	L, м	Вид отделки	S, м²	
9	Санузел гостевой 4,49 м²	ГКЛВ по каркасу П113, отм. +2,600; окраска, Tikkurila Luja 7, матовая, 2 слоя, подготовка Q3	Tikkurila V503	4,49	Облицовка плиткой, A8UZ, 600×1200×9 мм, клей C2 TE S1, затирка CG2WA	Atlas Concorde A8UZ	21,44	нет			Аналог: керамогранит ректифицированный под травертин, матовый, 600×600×9 мм; тип 2, отм. ЧП −0,015	4,49	Н стен 2615 (до потолка); гидроизоляция обмазочная, 2 слоя, по всему помещению, с заведением на стены 200 мм; у душа — на всю высоту стен душевой зоны и 500 мм за край душевой зоны (по пирогу пола); тест проливом и акт скрытых работ
	Итого			**127,29**			**287,56**			**97,3**		**127,29**	

Сводка площадей по материалам отделки

Поверхность	Материал / код цвета	Серия	Площадь, м²
Потолок	Tikkurila V503	Anti-Reflex 2	114,36
Потолок	Tikkurila V503	Luja 7	12,93
Стены	Farrow & Ball No. 15	Modern Emulsion	179,79
Стены	Farrow & Ball No. 34	Modern Emulsion	33,93
Стены	Tikkurila V503	Harmony	22,94
Стены	облицовка плиткой 600×1200×9 мм, Atlas Concorde A8UZ	A8UZ	50,20
Фартук	облицовка керамогранитом 1200×600×9 мм	аналог: керамогранит под травертин, матовый	0,70

Допущения и предложения на листе

Основа листа: размеры сняты с растрового плана заказчика с частичными размерами: рисунок не в масштабе, помещения выровнены по подписанным размерам мебели и проходов; контрольный обмер не выполнен (К-1); высота потолка 2700 мм принята: на плане заказчика её нет (К-2); толщины стен 300 / 120 мм приняты по плану заказчика, не замерены (К-1); разрешённая мощность 15 кВт принята по типовым ТУ для квартиры, ТУ заказчиком не переданы (К-4); подрайон климата не задан — принят не северный (жилые от 2,5 м) (К-6).

Знак «**» — предложение проектировщика, заказчиком не утверждено (согласовать с заказчиком): плинтус пом. 1–5, 8, фартук пом. 4 — артикул изделия не выбран: позиция описана характеристиками («аналог по характеристикам»), артикул выбирается при закупке; пол пом. 7, 9 — пирог пола: стяжка 33 мм и обмазочная гидроизоляция добавлены разработчиком проекта; артикул изделия не выбран: позиция описана характеристиками («аналог по характеристикам»), артикул выбирается при закупке.

См. лист открытых вопросов (лист 6, записи К-1, К-2, К-4, К-6).

Примечания

1. Площади поверхностей — по чистым граням стен до отделки: стены = периметр × высоту от чистого пола помещения до низа потолка минус проёмы (облицовка плиткой — до верха облицовки); плинтус = периметр минус дверные проёмы; пол и потолок — по площади помещения. Количество плиток по раскладке. Площади помещений — с учётом всех частей помещения; откосы в площадь стен не входят.
2. Акцентные стены и фартук — отдельными строками, их площадь вычтена из основной отделки стен помещения; фартук — над нижними модулями кухни от столешницы до низа навесных шкафов, где шкафов нет — на 600 мм.
3. Плинтус — длина по периметру за вычетом дверных проёмов; примыкания к наличникам и встроенной мебели — по развёрткам.
4. Формат плитки — Ш×В×Т (ширина × высота в положении укладки × толщина), мм; на полу — вдоль стен А/В × вдоль стен Б/Г.
5. Коды цвета — по веерам производителей; колеровка каждой краски одной партией, проверка выкраса при свете D65 и при лампах проекта.
6. Уровни подготовки Q1–Q4 — система Knauf, не норма ГОСТ/СП; допуски поверхностей — по СП 71.13330.2017 (действующая редакция).
7. «аналог:» — изделие задано характеристиками, марку и артикул согласовать с заказчиком до закупки.

Изм.	Кол.уч	Лист	№ док.	Подп.	Дата
Разраб.		Кырлан А.С.			04.11.26
Пров.					
ГИП					
Н. контр.					
Утв.					

ГД-2026-008-АИ

Квартира с кабинетом

Общая площадь 127,29* м² · * размеры со скана, не замерены (реестр — л. 6–8, К-1)

Дизайн-проект интерьера

Стадия	Лист	Листов
РП	60	131

Ведомость отделки помещений. Лист 2 из 2

М б/м

Кырлан Александр Сергеевич

Колерная карта

Цвета и материалы по помещениям · палитра проекта · выкрасы на согласование

ПРЕДВАРИТЕЛЬНО · не для производства работ · открыто пунктов: 13 (реестр — л. 6–8)

Колерная карта по помещениям

Помещение	Поверхность	Образец	Поз.	Система и код цвета	Производитель, линейка / материал, артикул	Блеск	Класс истирания	LRV	Площадь
1. Спальня 17,89 м²	стены		**К1**	Farrow & Ball No. 15	Farrow & Ball · Modern Emulsion	матовая	1	53	29,4 м²
	акцент А		**К2**	Farrow & Ball No. 34	Farrow & Ball · Modern Emulsion	матовая	1	22	6,5 м²
	потолок		**К3**	Tikkurila V503	Tikkurila · Anti-Reflex 2	глубокомат.	2	86	17,9 м²
	пол		**КМ1**	по образцу	Coswick · Вековые традиции · арт. 1167-4250				17,9 м²
	плинтус		**К4**	Farrow & Ball No. 15	МДФ · в цвет Farrow & Ball			53	16,2 м
2. Гардеробная-постирочная 5,11 м²	стены		**К5**	Tikkurila V503	Tikkurila · Harmony	матовая	1	86	22,9 м²
	потолок		**К3**	Tikkurila V503	Tikkurila · Anti-Reflex 2	глубокомат.	2	86	5,1 м²
	пол		**КМ1**	по образцу	Coswick · Вековые традиции · арт. 1167-4250				5,1 м²
	плинтус		**К6**	Tikkurila V503	МДФ · в цвет Tikkurila			86	8,3 м
3. Кабинет 18,92 м²	стены		**К1**	Farrow & Ball No. 15	Farrow & Ball · Modern Emulsion	матовая	1	53	33,0 м²
	акцент А		**К2**	Farrow & Ball No. 34	Farrow & Ball · Modern Emulsion	матовая	1	22	5,0 м²
	потолок		**К3**	Tikkurila V503	Tikkurila · Anti-Reflex 2	глубокомат.	2	86	18,9 м²
	пол		**КМ1**	по образцу	Coswick · Вековые традиции · арт. 1167-4250				18,9 м²
	плинтус		**К4**	Farrow & Ball No. 15	МДФ · в цвет Farrow & Ball			53	16,7 м
4. Кухня-гостиная 45,51 м²	стены		**К1**	Farrow & Ball No. 15	Farrow & Ball · Modern Emulsion	матовая	1	53	46,7 м²
	акцент А		**К2**	Farrow & Ball No. 34	Farrow & Ball · Modern Emulsion	матовая	1	22	14,9 м²
	потолок		**К3**	Tikkurila V503	Tikkurila · Anti-Reflex 2	глубокомат.	2	86	45,5 м²
	пол		**КМ1**	по образцу	Coswick · Вековые традиции · арт. 1167-4250				45,5 м²
	плинтус		**К4**	Farrow & Ball No. 15	МДФ · в цвет Farrow & Ball			53	25,9 м
	фартук		**КМ2**	по образцу	керамогранит · аналог по хар.				0,7 м²
5. Коридор 9,07 м²	стены		**К1**	Farrow & Ball No. 15	Farrow & Ball · Modern Emulsion	матовая	1	53	31,8 м²
	потолок		**К3**	Tikkurila V503	Tikkurila · Anti-Reflex 2	глубокомат.	2	86	9,1 м²
	пол		**КМ1**	по образцу	Coswick · Вековые традиции · арт. 1167-4250				9,1 м²
	плинтус		**К4**	Farrow & Ball No. 15	МДФ · в цвет Farrow & Ball			53	11,2 м
6. Детская 9,97 м²	стены		**К1**	Farrow & Ball No. 15	Farrow & Ball · Modern Emulsion	матовая	1	53	18,5 м²
	акцент А		**К2**	Farrow & Ball No. 34	Farrow & Ball · Modern Emulsion	матовая	1	22	7,4 м²
	потолок		**К3**	Tikkurila V503	Tikkurila · Anti-Reflex 2	глубокомат.	2	86	10,0 м²
	пол		**КМ1**	по образцу	Coswick · Вековые традиции · арт. 1167-4250				10,0 м²
	плинтус		**К7**	Farrow & Ball No. 15	Orac Decor · Contour (Luxxus)			53	12,0 м
7. Ванная 8,44 м²	стены		**КМ3**	Marvel Travertine	Atlas Concorde · арт. A8UZ				28,8 м²
	потолок		**К8**	Tikkurila V503	Tikkurila · Luja 7	матовая	1	86	8,4 м²
	пол		**КМ4**	по образцу	керамогранит · аналог по хар.				8,4 м²
8. Прихожая 7,89 м²	стены		**К1**	Farrow & Ball No. 15	Farrow & Ball · Modern Emulsion	матовая	1	53	20,4 м²
	потолок		**К3**	Tikkurila V503	Tikkurila · Anti-Reflex 2	глубокомат.	2	86	7,9 м²
	пол		**КМ5**	Marvel Travertine	Atlas Concorde · арт. A8UZ				7,9 м²
	плинтус		**К4**	Farrow & Ball No. 15	МДФ · в цвет Farrow & Ball			53	7,0 м
9. Санузел гостевой 4,49 м²	стены		**КМ3**	Marvel Travertine	Atlas Concorde · арт. A8UZ				21,4 м²
	потолок		**К8**	Tikkurila V503	Tikkurila · Luja 7	матовая	1	86	4,5 м²
	пол		**КМ4**	по образцу	керамогранит · аналог по хар.				4,5 м²

Схема палитры проекта


Стиль: Модерн (ар-нуво) 60% + Современный (контемпорари) 40% · схема: аналоговая

основной	основной	второстепенный	второстепенный	акцентный	акцентный	акцентный
Farrow & Ball No. 15	**Tikkurila V503**	**Farrow & Ball No. 34**	**Farrow & Ball No. 286**	**NCS S 5030-B10G**	**Farrow & Ball No. 66**	**NCS S 8010-Y30R**
Bone — мягкий каменно-серый с зеленцой LRV 53 стены 1,3,4,5,6,8; плинтус 1,3,4,5,6,8	Winter LRV 86 потолок 1,2,3,4,5,6,7,8,9; стены 2; плинтус 2; текстиль/декор 1,3,4,6	Calke Green — традиционный шалфей LRV 22 акцент 1,3,4,6; текстиль/декор 1,3,4,6	Peignoir — серо-розовый LRV 57 текстиль/декор 3,6	Павлиний сине-зелёный LRV 12 текстиль/декор 3,6	India Yellow — глубокая горчица LRV 36 текстиль/декор 3,4,6	Тёмно-коричневый LRV 3 в отделке не применён

План 60/30/10



Окраска, факт — по площади стен, акцентов, потолков

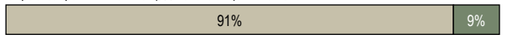

окрашено всего 364 м²; второстепенный тон несут мебель и текстиль

Текстиль и декор в цветах вне палитры проекта

- NCS S 2010-Y30R Тёплый льняной беж — пом. 1 (T1**, T27**, T4), 3 (T7), 4 (T13, T17), 6 (T20)
- NCS S 5020-G50Y Оливковый — пом. 1 (T3)

Условные обозначения

- **К1** Farrow & Ball No. 15 · Bone — мягкий каменно-серый с зеленцой · Modern Emulsion · матовая · кл. 1
- **К2** Farrow & Ball No. 34 · Calke Green — традиционный шалфей · Modern Emulsion · матовая · кл. 1
- **К3** Tikkurila V503 · Winter · Anti-Reflex 2 · глубокомат. · кл. 2
- **К4** Farrow & Ball No. 15 · Bone — мягкий каменно-серый с зеленцой · МДФ
- **К5** Tikkurila V503 · Winter · Harmony · матовая · кл. 1
- **К6** Tikkurila V503 · Winter · МДФ
- **К7** Farrow & Ball No. 15 · Bone — мягкий каменно-серый с зеленцой · Contour (Luxxus)
- **К8** Tikkurila V503 · Winter · Luja 7 · матовая · кл. 1
- дерево (доска, паркет, ламинат) — рисунок досок
- керамогранит, плитка, камень — сетка швов по формату
- **КМ1** инженерная доска · 1167-4250
- **КМ2** аналог: керамогранит под травертин, матовый, 1200×600×9 мм
- **КМ3** плитка · A8UZ
- **КМ4** аналог: керамогранит ректифицированный под травертин, матовый, 600×600×9 мм
- **КМ5** керамогранит · A8UZ

К — краска, КМ — отделочный материал (тон КМ — по описанию, эталон — образец материала); кл. — класс истирания (1 — самый стойкий к мытью); LRV — светлота цвета: 0 — чёрный, 100 — белый

Перечень выкрасов на согласование

№	Код	Бренд / веер	Пом. / стена	Подложка	Формат	Статус
1	No. 15	Farrow & Ball	1, 3, 4, 5, 6, 8	ГКЛ с грунтом; МДФ под эмаль	600×1000; 300×600	к выполнению
2	No. 34	Farrow & Ball	1 А, 3 А, 4 А, 6 А	ГКЛ с грунтом	600×1000	к выполнению
3	V503	Tikkurila	1, 2, 3, 4, 5, 6, 7, 8, 9	ГКЛ с грунтом; МДФ под эмаль	600×1000; 300×600	к выполнению

Примечания

1. Цвет на листе и на экране — ориентир. До покраски — выкрас на объекте: не меньше А3 (или лист ГКЛ), на грунте под эту краску, не на белой шпаклёвке, в 2 слоя; на обороте — код, бренд, веер, дата. Смотреть днём и вечером, рядом с образцами пола и плитки; к основному цвету стен — ещё 2 соседних оттенка. Красить только в цвет утверждённого выкраса.
2. Краску заказывать по коду из графы «Система и код цвета» у бренда этого кода, не «аналогом» другого; весь объём одного кода — одной партией, колеруемую краску — за один проход машины.
3. Площади — те же, что в ведомости отделки (лист 59); сколько краски заказать — в спецификации отделочных материалов (лист 62).

Допущения и предложения на листе. Основа листа: размеры сняты с растрового плана заказчика с частичными размерами: рисунок не в масштабе, помещения выровнены по подписанным размерам мебели и проходов; контрольный обмер не выполнен (К-1); высота потолка 2700 мм принята: на плане заказчика её нет (К-2); толщины стен 300 / 120 мм приняты по плану заказчика, не замерены (К-1); разрешённая мощность 15 кВт принята по типовым ТУ для квартиры, ТУ заказчиком не переданы (К-4); подрайон климата не задан — принят не северный (жилые от 2,5 м) (К-6). Знак «**» — предложение проектировщика, заказчиком не утверждено (согласовать с заказчиком): плинтус пом. 1–5, 8, фартук пом. 4 — артикул изделия не выбран: позиция описана характеристиками («аналог по характеристикам»), артикул выбирается при закупке; пол пом. 7, 9 — пирог пола: стяжка 33 мм и обмазочная гидроизоляция добавлены разработчиком проекта; артикул изделия не выбран: позиция описана характеристиками («аналог по характеристикам»), артикул выбирается при закупке; ИЗ-1: Т1 — Шина в нише штор (У1 +2,500, ниша +2,600 по всей стене А) — на окно 1 своя: 0…2300 по стене А (окно 500…2000: запас слева 500, справа 300 под пакет штор), вторая шина 2300…4600 — на окно 2 (Т27/Т28); вместе — длина ниши; Т27 — Шина на окно 2 в той же нише: 2300…4600 по стене А (окно 2600…4100: запас слева 300, справа 500); пара к Т1/Т2 на окне 1 — у обоих окон шторы, как на визуализации спальни. См. лист открытых вопросов (лист 6, записи К-1, К-2, К-4, К-6; лист 7, запись ИЗ-1).

Изм.	Кол.уч	Лист	№ док.	Подп.	Дата
Разраб.		Кырлан А.С.			04.11.26
Пров.					
ГИП					
Н. контр.					
Утв.					

ГД-2026-008-АИ

Квартира с кабинетом

Общая площадь 127,29* м² · * размеры со скана, не замерены (реестр — л. 6–8, К-1)

Дизайн-проект интерьера	Стадия	Лист	Листов
	РП	61	131
Колерная карта М б/м	**Кырлан Александр Сергеевич**		

выпуск 04.11.2026 № 4177cbe7a3 · стр. 68 из 166

Спецификация отделочных материалов

Форма 1 по ГОСТ 21.110-2013 · количества — из геометрии проекта, с запасом

ПРЕДВАРИТЕЛЬНО · не для производства работ · открыто пунктов: 13 (реестр — л. 6–8)

Поз.	Наименование и техническая характеристика	Тип, марка, обозначение документа	Код продукции	Поставщик	Ед. изм.	Кол.	Масса 1 ед., кг	Примечание
	Лакокрасочные материалы							
1	Краска интерьерная водно-дисперсионная акриловая для стен, матовая, класс мокрого истирания 1 по EN 13300, база A; цвет по вееру Farrow & Ball No. 15 «Bone — мягкий каменно-серый с зеленцой», колеровка машинная	Farrow & Ball Modern Emulsion		Farrow & Ball	л	50		поз. К1 колерной карты; пом. 1, 3, 4, 5, 6, 8; S = 179,8 м² × 2 сл. × 0,12 л/м² = 43,1 л, +10 % и 0,5 л на подкраску → ≥ 48,0 л; тара 10 × 5 л
2	Краска интерьерная водно-дисперсионная акриловая для акцентных стен, матовая, класс мокрого истирания 1 по EN 13300, база C; цвет по вееру Farrow & Ball No. 34 «Calke Green — традиционный шалфей», колеровка машинная	Farrow & Ball Modern Emulsion		Farrow & Ball	л	10		поз. К2 колерной карты; пом. 1, 3, 4, 6; S = 33,9 м² × 2 сл. × 0,12 л/м² = 8,1 л, +10 % и 0,5 л на подкраску → ≥ 9,5 л; тара 2 × 5 л
3	Краска интерьерная водно-дисперсионная акриловая для потолков, глубокоматовая, класс мокрого истирания 2 по EN 13300, база A; цвет по вееру Tikkurila V503 «Winter», колеровка машинная	Tikkurila Anti-Reflex 2		Tikkurila	л	31,5		поз. К3 колерной карты; пом. 1, 2, 3, 4, 5, 6, 8; S = 114,4 м² × 2 сл. × 0,12 л/м² = 27,4 л, +10 % и 0,5 л на подкраску → ≥ 30,7 л; тара 3 × 9 л + 1 × 2,7 л + 2 × 0,9 л
4	Краска интерьерная водно-дисперсионная акриловая для стен, матовая, класс мокрого истирания 1 по EN 13300, база A; цвет по вееру Tikkurila V503 «Winter», колеровка машинная	Tikkurila Harmony		Tikkurila	л	7,2		поз. К5 колерной карты; пом. 2; S = 22,9 м² × 2 сл. × 0,12 л/м² = 5,5 л, +10 % и 0,5 л на подкраску → ≥ 6,6 л; тара 2 × 2,7 л + 2 × 0,9 л
5	Краска интерьерная водно-дисперсионная акриловая для потолков, матовая, класс мокрого истирания 1 по EN 13300, база A; цвет по вееру Tikkurila V503 «Winter», колеровка машинная	Tikkurila Luja 7		Tikkurila	л	4,5		поз. К8 колерной карты; пом. 7, 9; S = 12,9 м² × 2 сл. × 0,12 л/м² = 3,1 л, +10 % и 0,5 л на подкраску → ≥ 3,9 л; тара 1 × 2,7 л + 2 × 0,9 л
6	Краска для МДФ и дерева в цвет Farrow & Ball No. 15 «Bone — мягкий каменно-серый с зеленцой» — окраска плинтуса; блеск не ниже блеска стен	марка не задана			л	2,3		поз. К4, К7; пом. 1, 3, 4, 5, 6, 8; L = 89,0 м, S = 8,4 м² × 2 сл. × 0,12 л/м² + 10 %; продукт подобрать в веере Farrow & Ball
7	Краска для МДФ и дерева в цвет Tikkurila V503 «Winter» — окраска плинтуса; блеск не ниже блеска стен	марка не задана			л	0,5		поз. К6; пом. 2; L = 8,3 м, S = 0,8 м² × 2 сл. × 0,12 л/м² + 10 %; продукт подобрать в веере Tikkurila
8	Грунтовка акриловая под окраску стен и потолков — из системы производителя краски	по системе краски			м²	364		площадь окраски стен, акцентов и потолков; 1 слой перед окраской; расход — по ТУ грунтовки
	Плитка и керамогранит							
9	Керамогранит под травертин, 600×600×9 мм, ректификат, водопоглощение 0,1 % (BIa), противоскольжение R10, PEI IV	аналог по характеристикам			м²	18,36		шов 2 мм; Ванная, пол; Санузел гостевой, пол; по раскладке 46 шт (S = 12,93 м²), с запасом 51 шт
10	A8UZ, 600×1200×9 мм, ректификат, водопоглощение 0,1 % (BIa), противоскольжение R10, PEI IV	A8UZ		Atlas Concorde	м²	111,60		шов 2 мм; Ванная, стены А–Г; Ванная, короб инсталляции; Санузел гостевой, стены А–Г; Санузел гостевой, короб инсталляции; Прихожая, пол; по раскладке 137 шт (S = 59,81 м²), с запасом 155 шт
11	Керамогранит под травертин, матовый, 1200×600×9 мм, ректификат, водопоглощение 0,1 % (BIa)	аналог по характеристикам			м²	2,16		шов 2 мм; Кухня-гостиная, фартук (ст. А); по раскладке 2 шт (S = 0,70 м²), с запасом 3 шт
	Напольные покрытия							
12	1167-4250, рабочий слой 4 мм, эмиссия E1, укладка на клей	1167-4250		Coswick	м²	114		пом. 1, 2, 3, 4, 5, 6; S = 106,47 м² + 7 % (прямая укладка); к заказу — кратно упаковке
13	Клей для паркета и инженерной доски, эластичный (СМП / полиуретановый)	по рекомендации производителя доски			м²	107		площадь приклейки; расход и шпатель — по ТУ клея
	Погонажные изделия							
14	Плинтус МДФ под покраску 80×16, крепление к стене, окраска в цвет Farrow & Ball No. 15	аналог по характеристикам			м	85		пом. 1, 3, 4, 5, 8; L = 77,0 м (периметр без дверных проёмов) + 10 % на подрезку; в штуках — по длине планки
15	Плинтус МДФ под покраску 80×16, крепление к стене, окраска в цвет Tikkurila V503	аналог по характеристикам			м	10		пом. 2; L = 8,3 м (периметр без дверных проёмов) + 10 % на подрезку; в штуках — по длине планки
16	SX165, h = 69 мм, крепление к стене, окраска в цвет Farrow & Ball No. 15	SX165		Orac Decor	м	14		пом. 6; L = 12,0 м (периметр без дверных проёмов) + 10 % на подрезку; в штуках — по длине планки
	Смеси и материалы для облицовки							
17	Затирка для швов плитки, класс CG2WA по EN 13888	Mapei Ultracolor Plus 132		Mapei	кг	6		по раскладке (a+b)/(a·b) × шов × t × 1,6 + 10 %; в т. ч. 0,7 кг — позиции раскладки без марки
18	Клей плиточный C2 TE S1 по EN 12004, слой 5 мм	Ceresit CM 17		Ceresit	кг	590		24 меш. по 25 кг; 1,5 кг/м² на 1 мм слоя + 10 %; в т. ч. 70 кг — позиции раскладки без марки
19	Гидроизоляция обмазочная мокрых зон: пол, стены по периметру, зоны замачивания; 2 слоя с армирующей лентой в углах	аналог по характеристикам			м²	33		площадь по листу раскладки плитки + 10 %; расход смеси — по ТУ
20	Лента демпферная по периметру пола из плитки	аналог по характеристикам			м	28		периметр без дверных проёмов + 10 %

Примечания

1. Количества — из геометрии проекта: площади поверхностей по чистым граням стен до отделки (те же, что в ведомости отделки и колерной карте), плитка, клей и затирка — по раскладке плиточника; в графе «Кол.» — к заказу, с запасом.
2. Краска: расход 0,12 л/м² на слой в 2 слоя, если по ТУ не задан иной; запас 10 % и 0,5 л на подкраску каждого кода. Один код — одна партия, колеровка машинная в колеровочном центре бренда; в заказ — только после утверждения выкраса (колерная карта). Фасовка — по каталогу бренда на дату выпуска; к заказу — не меньше расчётного объёма.
3. «Аналог по характеристикам» — допускается изделие другого производителя с характеристиками не ниже указанных, по согласованию с автором проекта.
4. Графы «Код продукции» и «Масса 1 ед.» не заполнены: коды по классификатору продукции не присвоены, масса единицы до 25 кг (ГОСТ 21.110-2013).
5. Грунтовка и клей для доски указаны площадью обработки; объём — по ТУ выбранного продукта.

Допущения и предложения на листе. Основа листа: размеры сняты с растрового плана заказчика с частичными размерами: рисунок не в масштабе, помещения выровнены по подписанным размерам мебели и проходов; контрольный обмер не выполнен (К-1); высота потолка 2700 мм принята: на плане заказчика её нет (К-2); толщины стен 300 / 120 мм приняты по плану заказчика, не замерены (К-1); разрешённая мощность 15 кВт принята по типовым ТУ для квартиры, ТУ заказчиком не переданы (К-4); подрайон климата не задан — принят не северный (жилые от 2,5 м) (К-6). Знак «**» — предложено, не утверждено (согласовать): плинтус пом. 1–5, 8, фартук пом. 4, пол пом. 7, 9. См. лист открытых вопросов (лист 6, записи К-1, К-2, К-4, К-6).

Изм.	Кол.уч	Лист	№ док.	Подп.	Дата
Разраб.		Кырлан А.С.			04.11.26
Пров.					
ГИП					
Н. контр.					
Утв.					

ГД-2026-008-АИ

Квартира с кабинетом

Общая площадь 127,29* м² · * размеры со скана, не замерены (реестр — л. 6–8, К-1)

Дизайн-проект интерьера

Стадия	Лист	Листов
РП	62	131

Спецификация отделочных материалов


М б/м

Кырлан Александр Сергеевич

выпуск 04.11.2026 № 4177cbe7a3 · стр. 69 из 166


Концепция декора и визуализации

Модерн (ар-нуво) · современный модерн · визуализации, палитра, материалы, ключевые предметы

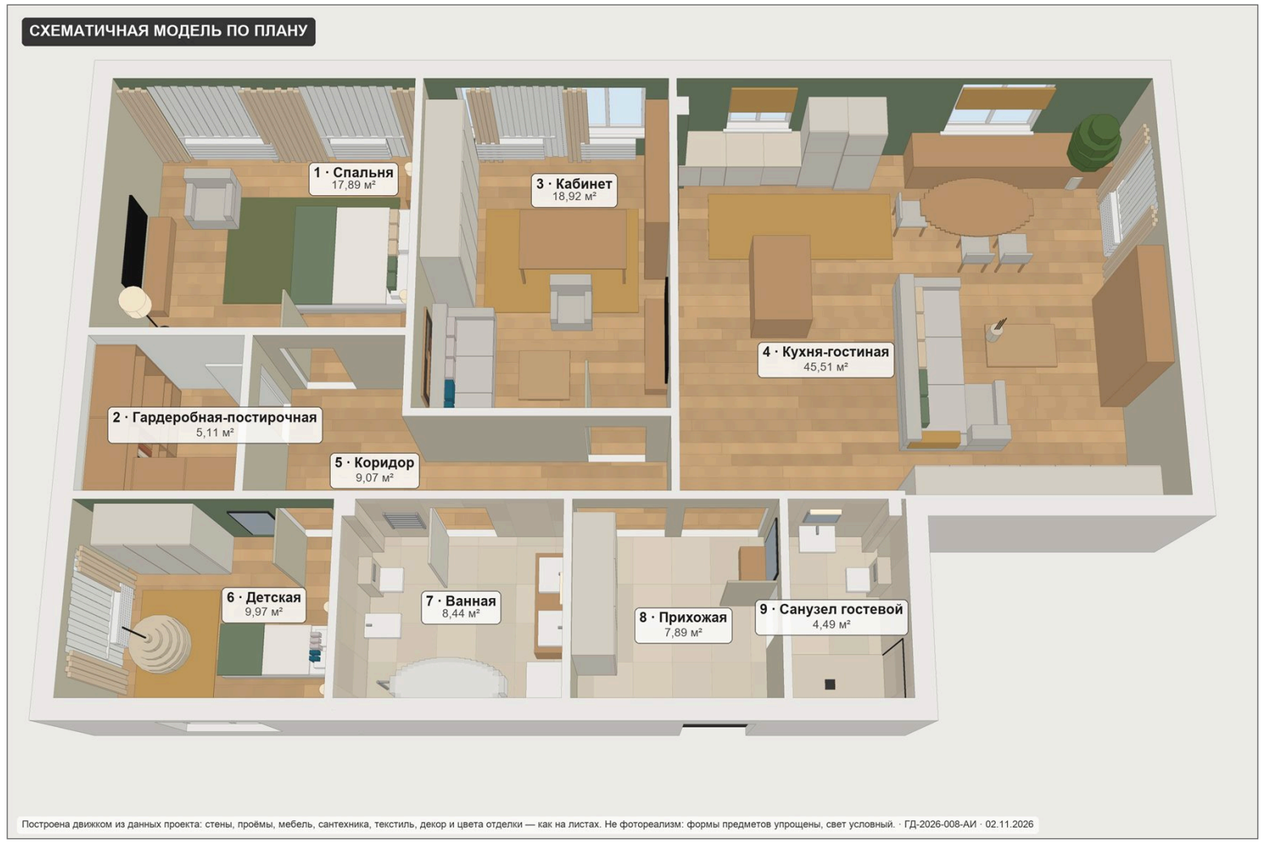

Визуализация 1. Вид сверху (3D), схематичная модель по плану: мебель, текстиль и декор из данных проекта

Расстановка — по плану мебели (лист 20); шторы, ковры, картины и растения — по плану текстиля и декора (лист 64).

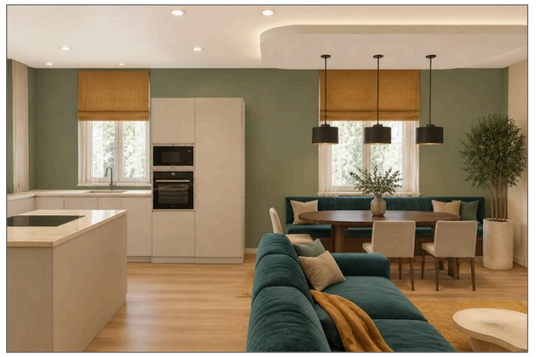

Визуализация 17. Кухня-гостиная (пом. 4)

шторы Т13, Т14, Т15, Т26 · ковёр Т16 · картина ДК6 · растение ДК7 · подушки, пледы Т17, Т18, Т19



Визуализация 7. Спальня (пом. 1)

шторы Т1**, Т2**, Т27**, Т28** · ковёр Т3 · картина ДК1 · подушки, пледы Т4, Т5, Т6



Визуализация 14. Детская (пом. 6)

шторы Т20, Т21 · ковёр Т22** · картина ДК2** · зеркало ДК5 · подушки, пледы Т23, Т24, Т25



Визуализация 21. Кабинет (пом. 3)

шторы Т7, Т8 · ковёр Т9 · картина ДК3 · зеркало ДК4 · подушки, пледы Т10, Т11, Т12

Палитра 60/30/10 и цвета текстиля



- Farrow & Ball No. 15 (Bone — мягкий каменно-серый с зеленцой), LRV 53 — 60 % база
- Farrow & Ball No. 34 (Calke Green — традиционный шалфей), LRV 22 — 30 % второй цвет — Т5, Т6, Т12, Т18, Т25
- NCS S 5030-B10G (Павлиний сине-зелёный), LRV 12 — 10 % акцент — Т11, Т24
- NCS S 8010-Y30R (Тёмно-коричневый), LRV 3 — 10 % акцент
- NCS S 5020-G50Y (Оливковый), LRV 18 — акцент текстиля — Т3
- Tikkurila V503 (Winter), LRV 86 — 60 % база — Т2, Т8, Т14, Т21, Т28
- Farrow & Ball No. 286 (Peignoir — серо-розовый), LRV 57 — 30 % второй цвет — Т10, Т23
- Farrow & Ball No. 66 (India Yellow — глубокая горчица), LRV 36 — 10 % акцент — Т9, Т15, Т16, Т19, Т22, Т26
- NCS S 2010-Y30R (Тёплый льняной беж), LRV 60 — текстиль — Т1, Т4, Т7, Т13, Т17, Т20, Т27

Материалы и фактуры



Дуб натуральный

пол: пом. 1, 2, 3, 4, 5, 6; рамы ДК1, ДК2**, ДК3



Травертин (керамогранит)

пол и стены санузлов, фартук: пом. 4, 7, 9



Букле

подушки: Т10, Т17, Т23



Лён

портьеры, подушки, римская штора: Т1**, Т4, Т7, Т13, Т15, Т20, Т26,



Бронза и чёрный металл

рамы ДК4, ДК5, ДК9 — чёрный; фурнитура, светильники — бронза

Ключевые предметы

— Диван Кб4 2150×950 — кабинет; подушки и плед Т10, Т11, Т12
— Диван Кх9** 1000×2700 — кухня-гостиная; подушки и плед Т17, Т18, Т19
— Кровати Дт2**, С1 — над изголовьем картины ДК1, ДК2**; текстиль Т4, Т5, Т6, Т23, Т24, Т25
— Ковры Т3, Т9, Т16, Т22** — шерсть, на противоскользящей подложке
— Картины ДК1, ДК2**, ДК3, ДК6 — центр на высоте 1350–1650 мм
— Зеркала в рост ДК4, ДК5, ДК9; над умывальниками ДК10**, ДК11**
— Шторы-волна Т1**, Т7, Т13, Т20, Т27** (NCS S 2010-Y30R), тюль Т2**, Т8, Т14, Т21, Т28** (Tikkurila V503) — в нишах потолка
— Растение ДК7, ваза ДК8

Допущения и предложения на листе. Основа листа: размеры сняты с растрового плана заказчика с частичными размерами: рисунок не в масштабе, помещения выровнены по подписанным размерам мебели и проходов; контрольный обмер не выполнен (К-1); высота потолка 2700 мм принята: на плане заказчика её нет (К-2); толщины стен 300 / 120 мм приняты по плану заказчика, не замерены (К-1); разрешённая мощность 15 кВт принята по типовым ТУ для квартиры, ТУ заказчиком не переданы (К-4); подрайон климата не задан — принят не северный (жилые от 2,5 м) (К-6). Знак «**» — предложено, не утверждено (согласовать): ДК10, ДК11; ИЗ-1: Т1, Т2, Т27, Т28, Кх9, Дт2, Т22, ДК2. См. лист открытых вопросов (лист 6, записи К-1, К-2, К-4, К-6; лист 7, запись ИЗ-1).

Настроение

Современный модерн 2026: модерн 60 % + современный 40 %. Стены — Bone No. 15, потолки — Winter V503, шалфей Calke Green No. 34 и пудровый Peignoir No. 286 вторым планом, акценты — павлиний S 5030-B10G (бархат), горчица India Yellow No. 66, морёный дуб S 8010-Y30R; металл — латунь. Настроение стиля: природность, плавность, камерность, ремесленность, поэтичность, приглушённая цветность, сумеречный тёплый свет. Свет тёплый, 2200–2700 K.

Примечания


1. Визуализации — образ интерьера. Изделия, размеры, высоты подвеса и привязки — по чертежам (план текстиля и декора — лист 64; шторы и карнизы — лист 65; ведомость текстиля — лист 66; ведомость декора и развеска — лист 67); при расхождении действуют чертежи и ведомости.
2. Коды цвета — ориентир подбора по веерам производителей; ткань утверждается по образцу при дневном свете и при свете проекта 2700–3000 K.
3. Мелкий стайлинг на визуализациях (книги, посуда, свечи) в ведомости не входит и поставляется заказчиком по желанию.

						ГД-2026-008-АИ	
						Квартира с кабинетом	
						Общая площадь 127,29* м² · * размеры со скана, не замерены (реестр — л. 6–8, К-1)	
Изм.	Кол.уч	Лист	№ док.	Подп.	Дата	Дизайн-проект интерьера	Стадия: РП; Лист: 63; Листов: 131
Разраб.		Кырлан А.С.			04.11.26		
Пров.							
ГИП							
						Концепция декора и визуализации	Кырлан Александр Сергеевич
Н. контр.						М б/м	
Утв.							

План текстиля и декора

Шторы и карнизы, ковры, картины и зеркала, растения · размеры в мм от чистовых стен и чистого пола · марки — по ведомостям

ПРЕДВАРИТЕЛЬНО · не для производства работ · открыто пунктов: 13 (реестр — л. 6–8)

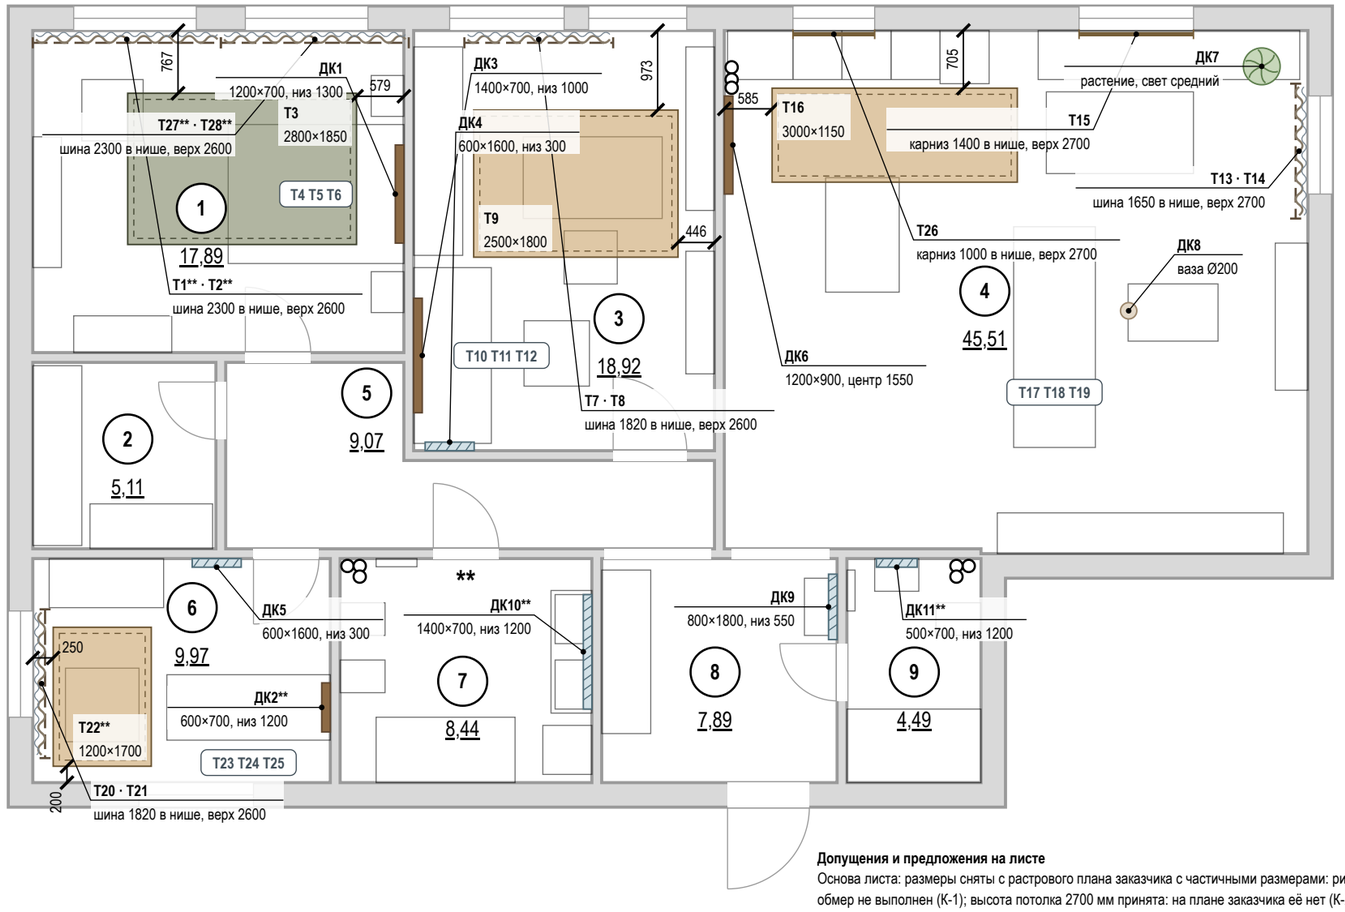

Условные обозначения

- ковёр — габарит в масштабе, цвет изделия
- шина или карниз штор (выше плоскости разреза)
- портьеры (штора-волна)
- тюль (на плане — волнистая линия)
- римская или рулонная штора в проёме
- картина на стене — ширина в масштабе
- зеркало на стене — ширина в масштабе
- растение в кашпо — диаметр в масштабе
- ваза, настольный декор
- подушки, пледы — марки на мебели
- привязка от чистовой стены, мм
- (1) номер помещения, площадь м²
- стены (подложка обмера)
- ** «**» — предложение проектировщика, заказчиком не утверждено

Т1, ДК1 — марки по ведомостям текстиля и декора

Экспликация помещений

лист 15 · на плане — номера в марках

Окна: шина → полотно, мм

Поз.	Шина	Верх шины	Полотно, низ
Т1**, Т2**	2300	2600, ниша	2590, низ 10
Т27**, Т28**	2300	2600, ниша	2590, низ 10
Т7, Т8	1820	2600, ниша	2590, низ 10
Т13, Т14	1650	2700, ниша	2690, низ 10
Т15	1400	2700, ниша	1700, низ 1000
Т26	1000	2700, ниша	1700, низ 1000
Т20, Т21	1820	2600, ниша	2590, низ 10

Допущения и предложения на листе

Основа листа: размеры сняты с растрового плана заказчика с частичными размерами: рисунок не в масштабе, помещения выровнены по подписанным размерам мебели и проходов; контрольный обмер не выполнен (К-1); высота потолка 2700 мм принята: на плане заказчика её нет (К-2); толщины стен 300 / 120 мм приняты по плану заказчика, не замерены (К-1); разрешённая мощность 15 кВт принята по типовым ТУ для квартиры, ТУ заказчиком не переданы (К-4); подрайон климата не задан — принят не северный (жилые от 2,5 м) (К-6).

Знак «**» — предложение проектировщика, заказчиком не утверждено (согласовать с заказчиком): ДК10 — Зеркало над умывальником — предмет света у зеркала (Св15 «настенный светильник над зеркалом») и место для лица у раковины; в данных его не было, светильник висел над сантехникой; ДК11 — Зеркало над умывальником — предмет света у зеркала (Св52 «настенный светильник над зеркалом») и место для лица у раковины; в данных его не было, светильник висел над сантехникой; ИЗ-1: Т1, Т2 — Шина в нише штор (У1 +2,500, ниша +2,600 по всей стене А) — на окно 1 своя: 0…2300 по стене А (окно 500…2000: запас слева 500, справа 300 под пакет штор), вторая шина 2300…4600 — на окно 2 (Т27/Т28); вместе — длина ниши; Т27, Т28 — Шина на окно 2 в той же нише: 2300…4600 по стене А (окно 2600…4100: запас слева 300, справа 500); пара к Т1/Т2 на окне 1 — у обоих окон шторы, как на визуализации спальни; Т22 — ковёр 1200 × 1700 у кресла-кокона вместо ковра 2500 × 1800 под кроватью: кровать в 520 мм от стены В, ковёр под ней не выходит за кровать на 450 мм и не оставляет 200 мм открытого пола у стены одновременно; ДК2 — низ 1200 = верх изголовья Дт2 1000 + 200 (150–250 над изголовьем, не над матрасом); ИЗ-2, К-5: дверь пом. 7 (стена А) — Проём сдвинут вдоль стены А от угла Б: offset 2300 → 1200 — утверждено автором (ИЗ-2, Кырлан А.С.).

См. лист открытых вопросов (лист 6, записи К-1, К-2, К-4–К-6; лист 7, записи ИЗ-1, ИЗ-2).

Примечания

1. Размеры — в мм. Отступы ковров — от чистовых стен; высоты картин и зеркал — от чистого пола до центра или низа рамы.
2. Шторы — на шинах в нишах потолка (ниша — план потолков, лист 48); закладная под шину — до обшивки ГКЛ. Схемы окон, длины полотен и сборка — лист 65.
3. Картины и зеркала массой более 5 кг — на анкеры по основанию, нагрузка крепежа не меньше двойной массы изделия; на ГКЛ — только по закладной. Декор не перекрывает розетки и выключатели.
4. Ковры на гладком полу — на противоскользящей подложке.
5. Мебель — по плану расстановки мебели (лист 20); ведомость текстиля — лист 66, ведомость декора и схемы развески — лист 67.
6. Номера помещений — по экспликации (лист 15); наименования и площади на этом листе не дублируются.
7. Марки текстиля «Т» и декора «Д» относятся только к листам текстиля и декора; индексы трубопроводов Т1–Т4 — на листах ВК и ОВ.

1000 мм · печать 1:1

Изм.	Кол.уч	Лист	№ док.	Подп.	Дата
Разраб.		Кырлан А.С.			04.11.26
Пров.					
ГИП					
Н. контр.					
Утв.					

ГД-2026-008-АИ

Квартира с кабинетом

Общая площадь 127,29* м² · * размеры со скана, не замерены (реестр — л. 6–8, К-1)

Дизайн-проект интерьера

Стадия	Лист	Листов
РП	64	131

План текстиля и декора

М 1:75

Кырлан Александр Сергеевич

выпуск 04.11.2026 № 4177cbe7a3 · стр. 71 из 166

08

Декор и текстиль


Кырлан Александр Сергеевич

выпуск 04.11.2026 № 4177cbe7a3 · стр. 72 из 166


Шторы и карнизы

Схемы окон «шина → полотно» (М 1:100) · отметки от чистого пола помещения · размеры в мм


Окно 1 — Спальня (пом. 1): Т1, Т2** (М 1:100)**

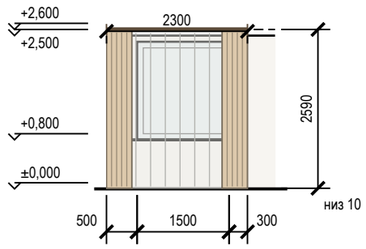


Окно 2 — Спальня (пом. 1): Т27, Т28** (М 1:100)**

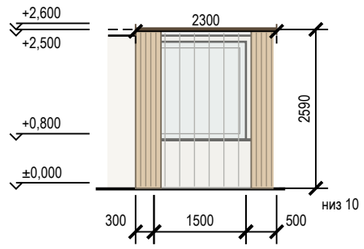


Окно 1 — Кабинет (пом. 3): Т7, Т8 (М 1:100)

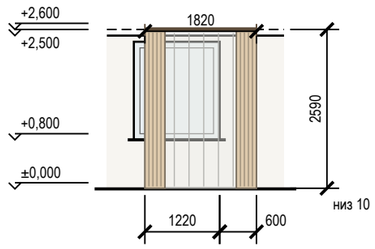


Окно 3 — Кухня-гостиная (пом. 4): Т13, Т14 (М 1:100)

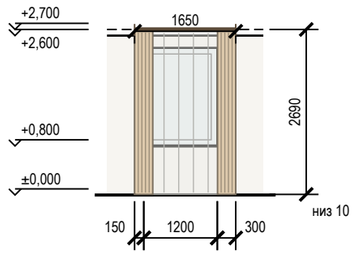


Окно 2 — Кухня-гостиная (пом. 4): Т15 (М 1:100)

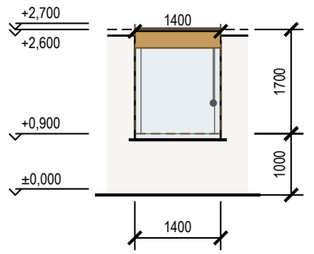

Окно 1 — Кухня-гостиная (пом. 4): Т26 (М 1:100)

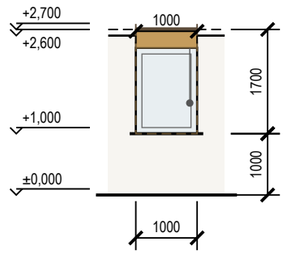

Окно 1 — Детская (пом. 6): Т20, Т21 (М 1:100)

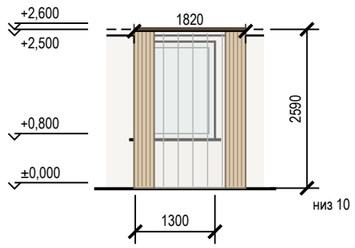

Карта окон: окно → шина → полотно

Поз.	Окно, пом.	Проём Ш×В, подоконник	Верх ниши	Изделие	Шина / карниз: длина, крепление	Верх шины	Полотно: длина, низ	Управление
Т1**	1, пом. 1	1500×1600, подок. 800	+2,600	портьеры	шина, 2300, в нише потолка, вынос 150	+2,600	2590, низ 10 (парит)	вручную
Т2**	1, пом. 1	1500×1600, подок. 800	+2,600	тюль	шина, 2300, в нише потолка, вынос 150	+2,600	2590, низ 10 (парит)	вручную
Т27**	2, пом. 1	1500×1600, подок. 800	+2,600	портьеры	шина, 2300, в нише потолка, вынос 150	+2,600	2590, низ 10 (парит)	вручную
Т28**	2, пом. 1	1500×1600, подок. 800	+2,600	тюль	шина, 2300, в нише потолка, вынос 150	+2,600	2590, низ 10 (парит)	вручную
Т7	1, пом. 3	1400×1600, подок. 800	+2,600	портьеры	шина, 1820, в нише потолка, вынос 150	+2,600	2590, низ 10 (парит)	вручную
Т8	1, пом. 3	1400×1600, подок. 800	+2,600	тюль	шина, 1820, в нише потолка, вынос 150	+2,600	2590, низ 10 (парит)	вручную
Т13	3, пом. 4	1200×1600, подок. 800	+2,700	портьеры	шина, 1650, в нише потолка, вынос 150	+2,700	2690, низ 10 (парит)	вручную
Т14	3, пом. 4	1200×1600, подок. 800	+2,700	тюль	шина, 1650, в нише потолка, вынос 150	+2,700	2690, низ 10 (парит)	вручную
Т15	2, пом. 4	1400×1600, подок. 900	+2,700	римская штора	карниз, 1400, в нише потолка, вынос 60	+2,700	1700, низ 1000	шнур, петля низом 1500, натяжитель
Т26	1, пом. 4	1000×1400, подок. 1000	+2,700	римская штора	карниз, 1000, в нише потолка, вынос 60	+2,700	1700, низ 1000	шнур, петля низом 1500, натяжитель
Т20	1, пом. 6	1300×1600, подок. 800	+2,600	портьеры	шина, 1820, в нише потолка, вынос 150	+2,600	2590, низ 10 (парит)	вручную
Т21	1, пом. 6	1300×1600, подок. 800	+2,600	тюль	шина, 1820, в нише потолка, вынос 150	+2,600	2590, низ 10 (парит)	вручную

Условные обозначения

- портьеры в открытом положении
- римская штора: сложена / опущена
- верх ниши под шторы в потолке
- тюль (на виде окна — прозрачная плашка)
- шина или карниз на отметке верха
- оконный проём

Допущения и предложения на листе

Основа листа: размеры сняты с растрового плана заказчика с частичными размерами: рисунок не в масштабе, помещения выровнены по подписанным размерам мебели и проходов; контрольный обмер не выполнен (К-1); высота потолка 2700 мм принята: на плане заказчика её нет (К-2); толщины стен 300 / 120 мм приняты по плану заказчика, не замерены (К-1); разрешённая мощность 15 кВт принята по типовым ТУ для квартиры, ТУ заказчиком не переданы (К-4); подрайон климата не задан — принят не северный (жилые от 2,5 м) (К-6).

Знак «**» — предложение проектировщика, заказчиком не утверждено (согласовать с заказчиком): ИЗ-1: Т1, Т2 — Шина в нише штор (У1 +2,500, ниша +2,600 по всей стене А) — на окно 1 своя: 0…2300 по стене А (окно 500…2000: запас слева 500, справа 300 под пакет штор), вторая шина 2300…4600 — на окно 2 (Т27/Т28); вместе — длина ниши; Т27, Т28 — Шина на окно 2 в той же нише: 2300…4600 по стене А (окно 2600…4100: запас слева 300, справа 500); пара к Т1/Т2 на окне 1 — у обоих окон шторы, как на визуализации спальни.

См. лист открытых вопросов (лист 6, записи К-1, К-2, К-4, К-6; лист 7, запись ИЗ-1).

Примечания

1. Отметки — от чистого пола помещения; размеры — мм.
2. Шины в нишах потолка: закладная (брус или профиль) по всей длине ниши — до обшивки ГКЛ; ниша и её отметка — узел ниши на плане потолков (лист 48).
3. Шина в нише — на отметке верха ниши (крепление к закладной в потолке ниши); длина полотна — от верха шины до чистого пола за вычетом зазора.
4. Полотно портьер «парит» над полом на 10 мм; сборка портьер — 2,0, тюля — 2,5 (ширина полотна — в ведомости текстиля).
5. Шнур римской шторы — с натяжителем, петля низом не ниже 1500 мм от пола (защита детей; EN 13120 — рекомендация).
6. Электрокарнизы не предусмотрены; при замене на электропривод — вывод кабеля в нише у края шины (задание электрику).
7. Марки изделий — по плану текстиля и декора (лист 64) и ведомости текстиля (лист 66).

Изм.	Кол.уч	Лист	№ док.	Подп.	Дата	ГД-2026-008-АИ		
						Квартира с кабинетом		
						Общая площадь 127,29* м² · * размеры со скана, не замерены (реестр — л. 6–8, К-1)		
Разраб.		Кырлан А.С.			04.11.26	Дизайн-проект интерьера	Стадия: РП	Лист: 65 / Листов: 131
Пров.								
ГИП								
Н. контр.						Шторы и карнизы	Кырлан Александр Сергеевич	
Утв.						М б/м		

выпуск 04.11.2026 № 4177cbe7a3 · стр. 73 из 166

ПРЕДВАРИТЕЛЬНО · не для производства работ · открыто пунктов: 13 (реестр — л. 6–8)

Ведомость текстиля

Шторы, тюль, римские шторы, ковры, подушки и пледы · размеры в мм · марки — по плану текстиля и декора

Текстиль: шторы, ковры, подушки, пледы

Поз.	Пом.	Изделие	Размер, мм	Ткань, состав, плотность	Сборка, ширина полотна		Цвет (система, код)	Кол.	Примечание
T1**	1	Портьеры-волна	шина 2300 × полотно 2590	лён с блэкаут-подкладкой; лён 100 %; 320 г/м²	× 2, ширина 4600		NCS S 2010-Y30R (Тёплый льняной беж)	2	низ 10 (парит); в нише потолка
T2**	1	Тюль	шина 2300 × полотно 2590	вуаль; полиэстер 100 %	× 2,5, ширина 5750		Tikkurila V503 (Winter)	1	низ 10 (парит); в нише потолка
T3	1	Ковёр под кроватью	2800×1850	шерсть, ручное ткачество; шерсть 80 %, хлопок 20 %			NCS S 5020-G50Y (Оливковый)	1	противоскользящая подложка; ворс 10 мм
T4	1	Подушки декоративные на кровать	500×500	лён 100 %			NCS S 2010-Y30R (Тёплый льняной беж)	3	на C1
T5	1	Подушки на кровать, акцент	400×600	хлопковый бархат 100 %			Farrow & Ball No. 34 (Calke Green традиционный шалфей)	2	на C1
T6	1	Плед на кровать	1300×1700	шерсть мериноса 100 %			Farrow & Ball No. 34 (Calke Green традиционный шалфей)	1	на C1
T7	3	Портьеры-волна	шина 1820 × полотно 2590	лён с блэкаут-подкладкой; лён 100 %; 320 г/м²	× 2, ширина 3640		NCS S 2010-Y30R (Тёплый льняной беж)	2	низ 10 (парит); в нише потолка
T8	3	Тюль	шина 1820 × полотно 2590	вуаль; полиэстер 100 %	× 2,5, ширина 4550		Tikkurila V503 (Winter)	1	низ 10 (парит); в нише потолка
T9	3	Ковёр под кроватью	2500×1800	шерсть, плоское плетение; шерсть 100 %			Farrow & Ball No. 66 (India Yellow — глубокая горчица)	1	противоскользящая подложка; ворс 8 мм
T10	3	Подушки декоративные на кровать	500×500	букле (шерсть 60 %, полиэстер 40 %)			Farrow & Ball No. 286 (Peignoir — серо-розовый)	3	на K64
T11	3	Подушки на кровать, акцент	400×600	хлопковый бархат 100 %			NCS S 5030-B10G (Павлиний сине-зелёный)	2	на K64
T12	3	Плед на кровать	1300×1700	шерсть мериноса 100 %			Farrow & Ball No. 34 (Calke Green традиционный шалфей)	1	на K64
T13	4	Портьеры-волна (гостиная)	шина 1650 × полотно 2690	лён 70 %, вискоза 30 %; 280 г/м²	× 2, ширина 3300		NCS S 2010-Y30R (Тёплый льняной беж)	2	низ 10 (парит); в нише потолка
T14	4	Тюль (гостиная)	шина 1650 × полотно 2690	вуаль; полиэстер 100 %	× 2,5, ширина 4125		Tikkurila V503 (Winter)	1	низ 10 (парит); в нише потолка
T15	4	Римская штора (кухня)	карниз 1400 × полотно 1700	лён 100 %			Farrow & Ball No. 66 (India Yellow — глубокая горчица)	1	низ 1000; в нише потолка; шнур: петля 1500, натяжитель
T16	4	Ковёр в зоне отдыха	3000×1150	шерсть, петля; шерсть 100 %			Farrow & Ball No. 66 (India Yellow — глубокая горчица)	1	противоскользящая подложка; ворс низкий
T17	4	Подушки на диван	500×500	букле (шерсть 60 %, полиэстер 40 %)			NCS S 2010-Y30R (Тёплый льняной беж)	3	на Kx9**
T18	4	Подушки на диван, акцент	400×600	хлопковый бархат 100 %			Farrow & Ball No. 34 (Calke Green традиционный шалфей)	2	на Kx9**
T19	4	Плед на диван	1300×1700	альпака 50 %, шерсть 50 %			Farrow & Ball No. 66 (India Yellow — глубокая горчица)	1	на Kx9**
T20	6	Портьеры-волна	шина 1820 × полотно 2590	лён с блэкаут-подкладкой; лён 100 %; 320 г/м²	× 2, ширина 3640		NCS S 2010-Y30R (Тёплый льняной беж)	2	низ 10 (парит); в нише потолка
T21	6	Тюль	шина 1820 × полотно 2590	вуаль; полиэстер 100 %	× 2,5, ширина 4550		Tikkurila V503 (Winter)	1	низ 10 (парит); в нише потолка
T22**	6	Ковёр у кресла-кокона (зона чтения)	1200×1700	шерсть, плоское плетение; шерсть 100 %			Farrow & Ball No. 66 (India Yellow — глубокая горчица)	1	противоскользящая подложка; ворс 8 мм
T23	6	Подушки декоративные на кровать	500×500	букле (шерсть 60 %, полиэстер 40 %)			Farrow & Ball No. 286 (Peignoir — серо-розовый)	3	на Дт2**
T24	6	Подушки на кровать, акцент	400×600	хлопковый бархат 100 %			NCS S 5030-B10G (Павлиний сине-зелёный)	2	на Дт2**
T25	6	Плед на кровать	1300×1700	шерсть мериноса 100 %			Farrow & Ball No. 34 (Calke Green традиционный шалфей)	1	на Дт2**
T26	4	Римская штора (кухня, окно над рабочей зоной)	карниз 1000 × полотно 1700	лён 100 %			Farrow & Ball No. 66 (India Yellow — глубокая горчица)	1	низ 1000; в нише потолка; шнур: петля 1500, натяжитель
T27**	1	Портьеры-волна	шина 2300 × полотно 2590	лён с блэкаут-подкладкой; лён 100 %; 320 г/м²	× 2, ширина 4600		NCS S 2010-Y30R (Тёплый льняной беж)	2	низ 10 (парит); в нише потолка
T28**	1	Тюль	шина 2300 × полотно 2590	вуаль; полиэстер 100 %	× 2,5, ширина 5750		Tikkurila V503 (Winter)	1	низ 10 (парит); в нише потолка

образец цвета — по HEX производителя краски, справочно

Итого: шторы и тюль — 17 шт.; ковры и дорожки — 4 шт.; подушки, пледы, покрывала — 24 шт.

Примечания

1. Коды цвета — ориентир подбора по веерам производителей красок; ткань утверждается по образцу при дневном свете и при свете проекта 2700–3000 K.
2. Размеры полотен — по замеру после чистовой отделки пола и потолка; ширина полотна указана с учётом сборки, без припусков на швы. Схемы окон и отметки шин лист 65.
3. Портьеры и тюль — на тесьме «волна» по системе шины; блэкаут — подкладкой. Ковры — на противоскользящей подложке.
4. Замена изделия — аналогом по характеристикам (состав, плотность, размер, цвет по образцу) с согласованием автора проекта.
5. Места изделий — план текстиля и декора (лист 64); подушки и пледы — по марке мебели.

Допущения и предложения на листе. Основа листа: размеры сняты с растрового плана заказчика с частичными размерами: рисунок не в масштабе, помещения выровнены по подписанным размерам мебели и проходов; контрольный обмер не выполнен (К-1); высота потолка 2700 мм принята: на плане заказчика её нет (К-2); толщины стен 300 / 120 мм приняты по плану заказчика, не замерены (К-1); разрешённая мощность 15 кВт принята по типовым ТУ для квартиры, ТУ заказчиком не переданы (К-4); подрайон климата не задан — принят не северный (жилые от 2,5 м) (К-6). Знак «**» — предложено, не утверждено (согласовать): ИЗ-1: T1, T2, T27, T28, Kx9, Дт2, T22. См. лист открытых вопросов (лист 6, записи К-1, К-2, К-4, К-6; лист 7, запись ИЗ-1).

Изм.	Кол.уч	Лист	№ док.	Подп.	Дата
Разраб.		Кырлан А.С.			04.11.26
Пров.					
ГИП					
Н. контр.					
Утв.					

ГД-2026-008-АИ

Квартира с кабинетом

Общая площадь 127,29* м² · * размеры со скана, не замерены (реестр — л. 6–8, К-1)

Дизайн-проект интерьера

Стадия	Лист	Листов
РП	66	131

Ведомость текстиля

М б/м

Кырлан Александр Сергеевич

выпуск 04.11.2026 № 4177cbe7a3 · стр. 74 из 166

Ведомость декора. Схемы развески

ПРЕДВАРИТЕЛЬНО · не для производства работ · открыто пунктов: 13 (реестр — л. 6–8)


Картины, зеркала, растения, настольный декор · схемы развески (М 1:50) · высоты — мм от чистого пола

Декор: картины, зеркала, растения, предметы


картина · зеркало · мебель под изделием

Поз.	Пом.	Предмет	Размер, мм	Место: стена, высота от пола, мм	Масса, кг	Крепёж и основание	Свет места, отделка	Кол.
ДК1	1	Картина над кроватью	1200×700	стена Б, привязка 1400; низ 1300, центр 1650; над С1	4	подвес по основанию, 2 точки	рама — дуб	1
ДК2**	6	Картина над кроватью	600×700	стена Б, привязка 1520; низ 1200, центр 1550; над Дт2**	4	подвес по основанию, 2 точки	рама — дуб	1
ДК3	3	Картина над диваном	1400×700	стена Г, привязка 3275; низ 1000, центр 1350; над К64	4	подвес по основанию, 2 точки	рама — дуб	1
ДК4	3	Зеркало в рост в тонкой чёрной раме	600×1600	стена В, привязка 140; низ 300, центр 1100	12	анкер для пустотелых оснований, 4 шт.; основание: перегородка — определить обмером до монтажа; нагрузка 30 кг	рама — чёрный матовый металл	1
ДК5	6	Зеркало в рост в тонкой чёрной раме	600×1600	стена А, привязка 1950; низ 300, центр 1100	12	анкер для пустотелых оснований, 4 шт.; основание: перегородка — определить обмером до монтажа; нагрузка 30 кг	рама — чёрный матовый металл	1
ДК6	4	Картина	1200×900	стена Г, привязка 800; центр 1550	6	анкер, 2 шт.; основание: перегородка — определить обмером до монтажа; нагрузка 15 кг		1
ДК7	4	Растение	450×450	напольное			свет средний	1
ДК8	4	Ваза керамическая с ветками на обеденном столе	200×350	на Кх8** (обеденный стол)				1
ДК9	8	Зеркало	800×1800	стена Б, привязка 190; низ 550, центр 1450	18	анкер, 4 шт.; основание: перегородка — определить обмером до монтажа; нагрузка 40 кг	рама — чёрный матовый металл	1
ДК10**	7	Зеркало над умывальниками, влагостойкое, в тонкой латунной раме	1400×700	стена Б, привязка 440; низ 1200, центр 1550; над Вн1**	12	клей для зеркал + 2 опорных уголка снизу, анкеры по основанию; основание: стена под керамогранитом — основание определить обмером до монтажа; нагрузка 30 кг		1
ДК11**	9	Зеркало над умывальником, влагостойкое, в тонкой латунной раме	500×700	стена А, привязка 360; низ 1200, центр 1550; над П12	5	клей для зеркал + 2 опорных уголка снизу; основание: стена под керамогранитом — основание — определить обмером до монтажа; нагрузка 15 кг		1


ДК1 — Спальня (пом. 1), стена Б (М 1:50)

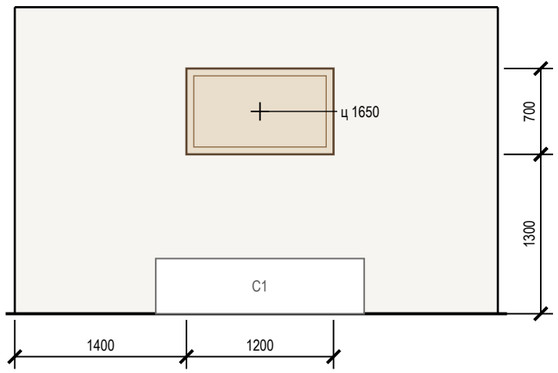


ДК2 — Детская (пом. 6), стена Б (М 1:50)**

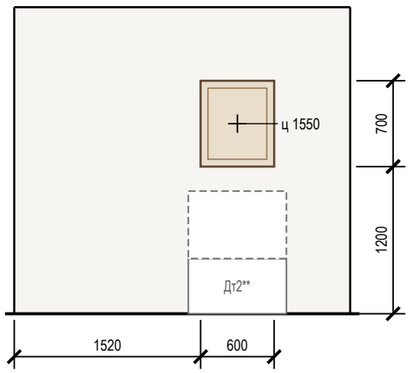

ДК3 — Кабинет (пом. 3), стена Г (М 1:50)

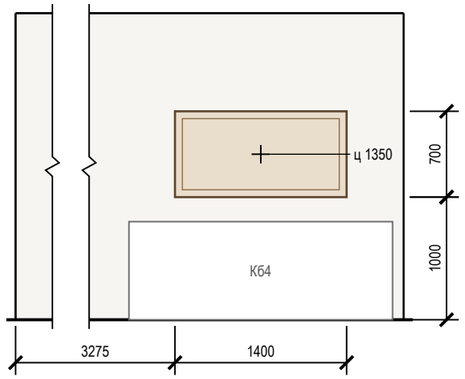

ДК4 — Кабинет (пом. 3), стена В (М 1:50)

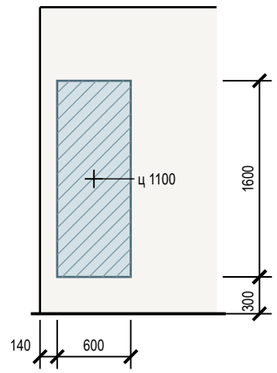

Допущения и предложения на листе

Основа листа: размеры сняты с растрового плана заказчика с частичными размерами: рисунок не в масштабе, помещения выровнены по подписанным размерам мебели и проходов; контрольный обмер не выполнен (К-1); высота потолка 2700 мм принята: на плане заказчика её нет (К-2); толщины стен 300 / 120 мм приняты по плану заказчика, не замерены (К-1); разрешённая мощность 15 кВт принята по типовым ТУ для квартиры, ТУ заказчиком не переданы (К-4); подрайон климата не задан — принят не северный (жилые от 2,5 м) (К-6).

Знак «**» — предложение проектировщика, заказчиком не утверждено (согласовать с заказчиком): ДК10 — Зеркало над умывальником — предмет света у зеркала (Св15 «настенный светильник над зеркалом») и место для лица у раковины; в данных его не было, светильник висел над сантехникой; ДК11 — Зеркало над умывальником — предмет света у зеркала (Св52 «настенный светильник над зеркалом») и место для лица у раковины; в данных его не было, светильник висел над сантехникой; ИЗ-1: Кх8 — 6 мест: банкетка Кх7 на 3 места и 3 стула (2 со свободной стороны, 1 у торца) вместо 6 стульев — со стороны банкетки стул не отодвинуть; Дт2 — кровать 800 × 2000 у стены Б, 1480 мм от угла с дверью: вне радиатора РО-9, от открытого полотна Д-5 до кровати 620 мм прохода, вдоль кровати к окну 520 мм; ДК2 — низ 1200 = верх изголовья Дт2 1000 + 200 (150–250 над изголовьем, не над матрасом); ИЗ-2: Вн1 — Тумба 1500 под раковины П2 и П3 — по описанию модели автора («две на тумбе 1500»): ширина из модели, глубина 500 под раковины 450 и высота столешницы 700 под борт раковин 850, тумба напольная — низ на чистом полу (elevation 0) — предложение проектировщика; выводы ВК под раковинами закрывает тумба.

См. лист открытых вопросов (лист 6, записи К-1, К-2, К-4, К-6; лист 7, записи ИЗ-1, ИЗ-2).

Примечания

1. Высоты — от чистого пола помещения до низа изделия, «ц» — до центра; привязки — от чистовой грани угла стены, мм.
2. Над мебелью низ изделия — на 150–250 мм выше спинки или изголовья; без мебели центр — на 1450–1600 мм от пола.
3. Изделия до 5 кг — на два подвеса по основанию; тяжелее — на анкеры с нагрузкой не меньше двойной массы; на ГКЛ — только по закладной или анкеру для пустотелых оснований.
4. Зеркала в рост — с креплением от опрокидывания; в санузлах — влагостойкие, на клей для зеркал и нейтральный силикон.
5. Места изделий — план текстиля и декора (лист 64). Схемы развески остальных изделий — лист 68.

Изм.	Кол.уч	Лист	№ док.	Подп.	Дата
Разраб.		Кырлан А.С.			04.11.26
Пров.					
ГИП					
Н. контр.					
Утв.					

ГД-2026-008-АИ

Квартира с кабинетом

Общая площадь 127,29* м² · * размеры со скана, не замерены (реестр — л. 6–8, К-1)

Дизайн-проект интерьера

Стадия	Лист	Листов
РП	67	131

Ведомость декора. Схемы развески

М б/м

Кырлан Александр Сергеевич

выпуск 04.11.2026 № 4177cbe7a3 · стр. 75 из 166


Схемы развески (продолжение)

Схемы развески картин и зеркал (М 1:50) · высоты — мм от чистого пола


Ведомость декора (размер, масса, крепёж и основание) — лист 67

картина · зеркало · мебель под изделием


ДК5 — Детская (пом. 6), стена А (М 1:50)

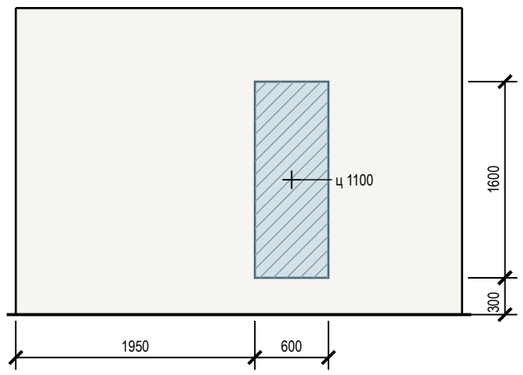


ДК6 — Кухня-гостиная (пом. 4), стена Г (М 1:50)

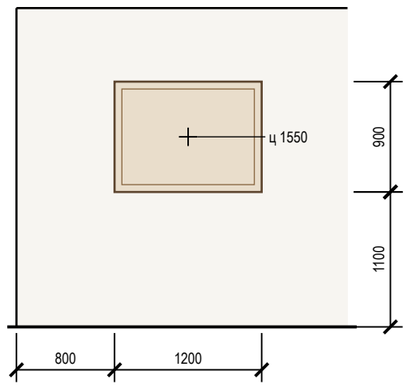


ДК9 — Прихожая (пом. 8), стена Б (М 1:50)

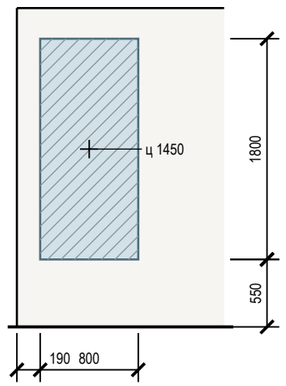

ДК10 — Ванная (пом. 7), стена Б (М 1:50)**

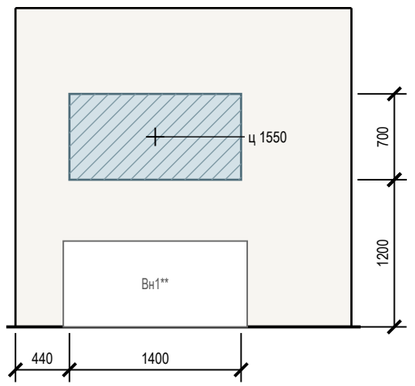

ДК11 — Санузел гостевой (пом. 9), стена А (М 1:50)**

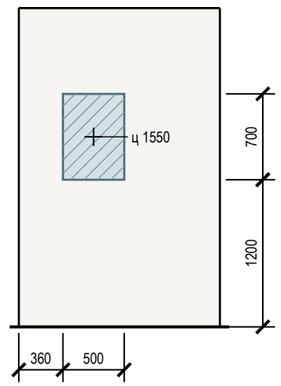

Допущения и предложения на листе

Основа листа: размеры сняты с растрового плана заказчика с частичными размерами: рисунок не в масштабе, помещения выровнены по подписанным размерам мебели и проходов; контрольный обмер не выполнен (К-1); высота потолка 2700 мм принята: на плане заказчика её нет (К-2); толщины стен 300 / 120 мм приняты по плану заказчика, не замерены (К-1); разрешённая мощность 15 кВт принята по типовым ТУ для квартиры, ТУ заказчиком не переданы (К-4); подрайон климата не задан — принят не северный (жилые от 2,5 м) (К-6).

Знак «**» — предложение проектировщика, заказчиком не утверждено (согласовать с заказчиком): ДК10 — Зеркало над умывальником — предмет света у зеркала (Св15 «настенный светильник над зеркалом») и место для лица у раковины; в данных его не было, светильник висел над сантехникой; ДК11 — Зеркало над умывальником — предмет света у зеркала (Св52 «настенный светильник над зеркалом») и место для лица у раковины; в данных его не было, светильник висел над сантехникой; ИЗ-2: Вн1 — Тумба 1500 под раковины П2 и П3 — по описанию модели автора («две на тумбе 1500»): ширина из модели, глубина 500 под раковины 450 и высота столешницы 700 под борт раковин 850, тумба напольная — низ на чистом полу (elevation 0) — предложение проектировщика; выводы ВК под раковинами закрывает тумба.

См. лист открытых вопросов (лист 6, записи К-1, К-2, К-4, К-6; лист 7, запись ИЗ-2).

Примечания

1. Высоты — от чистого пола помещения до низа изделия, «ц» — до центра; привязки — от чистовой грани угла стены, мм.
2. Над мебелью низ изделия — на 150–250 мм выше спинки или изголовья; без мебели центр — на 1450–1600 мм от пола.
3. Изделия до 5 кг — на два подвеса по основанию; тяжелее — на анкеры с нагрузкой не меньше двойной массы; на ГКЛ — только по закладной или анкеру для пустотелых оснований.
4. Зеркала в рост — с креплением от опрокидывания; в санузлах — влагостойкие, на клей для зеркал и нейтральный силикон.
5. Места изделий — план текстиля и декора (лист 64). Ведомость декора: размер, масса, крепёж и основание — лист 67.

Изм.	Кол.уч	Лист	№ док.	Подп.	Дата
Разраб.		Кырлан А.С.			04.11.26
Пров.					
ГИП					
Н. контр.					
Утв.					

ГД-2026-008-АИ

Квартира с кабинетом

Общая площадь 127,29* м² · * размеры со скана, не замерены (реестр — л. 6–8, К-1)

Дизайн-проект интерьера

Стадия	Лист	Листов
РП	68	131

Схемы развески (продолжение)


М б/м

Кырлан Александр Сергеевич

Встроенная мебель. Схема расположения

встроенная и корпусная мебель на заказ, кухонный гарнитур · размеры в мм · марки — по ведомости изделий

ПРЕДВАРИТЕЛЬНО · не для производства работ · открыто пунктов: 13 (реестр — л. 6–8)

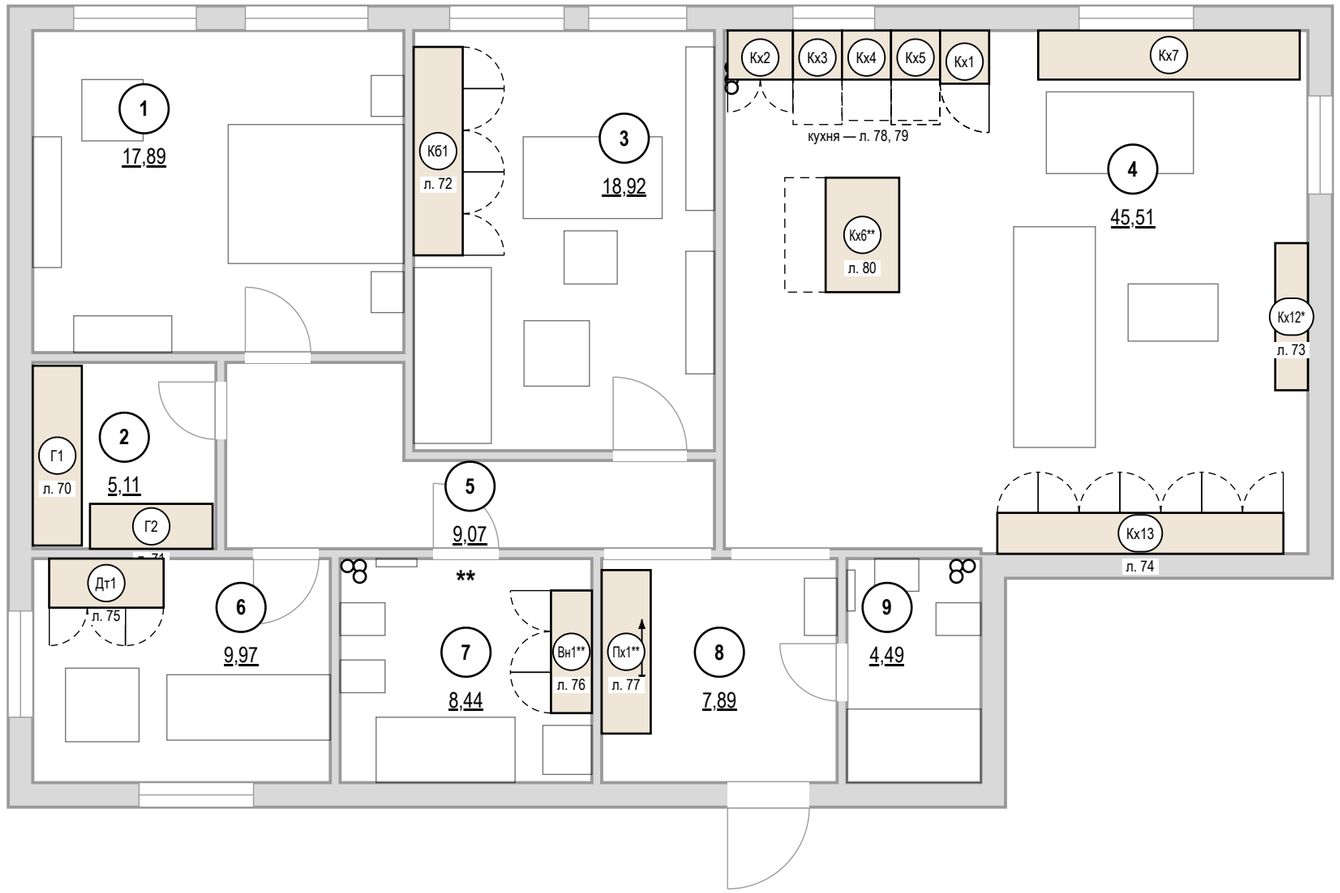

Ведомость изделий

Марка	Наименование	Пом.	Ш×Г×В, мм	Лист
Г1	Система хранения	2	2200×600×2400	70
Г2	Система хранения	2	1500×550×2400	71
Кб1	Шкаф распашной	3	2550×600×2400	72
Кх12*	ТВ-стена	4	1800×400×2500	73
Кх13	Шкаф распашной	4	3500×500×2400	74
Дт1	Шкаф распашной	6	1400×600×2400	75
Вн1**	Тумба под раковину	7	1500×500×700	76
Пх1**	Шкаф-купе	8	2000×600×2500	77
Кх2	Модуль нижний: мойка	4	800×600×900	78
Кх3	Модуль под ПММ 60: без корпуса, фасад на дверь машины	4	600×600×900	78
Кх4	Модуль нижний: ящики	4	600×600×900	78
Кх5	Пенал: духовой шкаф, СВЧ	4	600×600×2100	78
Кх1	Пенал: холодильник встр.	4	600×650×2100	78
Кх6**	Остров	4	1400×900×900	80
Кх7	банкетка-диван вдоль окон — экран радиатора	4	3200×600×850	

Условные обозначения

- изделие мебельщика: корпус на полу
- невидимый контур: навесной модуль, корпус под столешницей
- открывание распашного фасада
- зона выдвижения ящика, двери техники
- дверь купе, стрелка — направление движения
- К1 — марка изделия или модуля (на схеме расположения под ней — лист изделия)
- ** — «**» — предложение проектировщика, заказчиком не утверждено

Допущения и предложения на листе. Основа листа: размеры сняты с растрового плана заказчика с частичными размерами: рисунок не в масштабе, помещения выровнены по подписанным размерам мебели и проходов; контрольный обмер не выполнен (К-1); высота потолка 2700 мм принята: на плане заказчика её нет (К-2); толщины стен 300 / 120 мм приняты по плану заказчика, не замерены (К-1); разрешённая мощность 15 кВт принята по типовым ТУ для квартиры, ТУ заказчиком не переданы (К-4); подрайон климата не задан — принят не северный (жилые от 2,5 м) (К-6). Знак «*» — принято, не замерено и не подтверждено (замерить на объекте): ИЗ-5, ИЗ-9, К-20: Кх12 — Было: предмет 1800×400 h 500 на отметке 0 — на развёртке стены Б низкий короб у пола. Знак «**» — предложение проектировщика, заказчиком не утверждено (согласовать с заказчиком): ИЗ-1: Пх1 — фасад купе по кадру визуализации прихожей: МДФ 10 мм, эмаль матовая, латунный профиль, зеркальные арочные вставки (поле 100 мм); ИЗ-2: Вн1 — Тумба 1500 под раковины П2 и П3 — по описанию модели автора («две на тумбе 1500»): ширина из модели, глубина 500 под раковины 450 и высота столешницы 700 под борт раковин 850, тумба напольная — низ на чистом полу (elevation 0) — предложение проектировщика; выводы ВК под раковинами закрывает тумба; ИЗ-8: Кх6 — Остров сдвинут от кухонного ряда: торец острова стоял в 900 мм от фронта ПММ Кх3 и модуля Кх4 — меньше 1000 мм (СП 31-107-2004, п. 6.1.12) и меньше 1200 мм, при которых открытые ПММ и ящики не перекрывают проход. См. лист открытых вопросов (лист 6, записи К-1, К-2, К-4–К-6; лист 7, записи ИЗ-1, ИЗ-2, К-20; лист 8, записи ИЗ-5, ИЗ-8, ИЗ-9).

Примечания

1. Изделия — по чистовым размерам помещений; перед раскроем — контрольный замер цеха после чистовой отделки стен, пола и потолка.
2. Открывание фасадов и выдвижение ящиков показано в открытом положении: зоны не пересекают двери, радиаторы, выключатели и проходы.
3. Стояки и счётчики за мебелью — с сервисным люком; газовые трубы мебелью не зашиваются.
4. Покупная мебель — по плану расстановки мебели и спецификации дизайнера; здесь — подложкой.

1000 мм · печать 1:1

Изм.	Кол.уч	Лист	№ док.	Подп.	Дата
Разраб.		Кырлан А.С.			04.11.26
Пров.					
ГИП					
Н. контр.					
Утв.					

ГД-2026-008-АИ

Квартира с кабинетом

Общая площадь 127,29* м² · * размеры со скана, не замерены (реестр — л. 6–8, К-1)


Дизайн-проект интерьера	Стадия	Лист	Листов
	РП	69	131
Встроенная мебель. Схема расположения М 1:75	**Кырлан Александр Сергеевич**		

Система хранения Г1


Гардеробная-постирочная (пом. 2) · вид из помещения · размеры в мм, отметки в м

ПРЕДВАРИТЕЛЬНО · не для производства работ · открыто пунктов: 13 (реестр — л. 6–8)


Общий вид

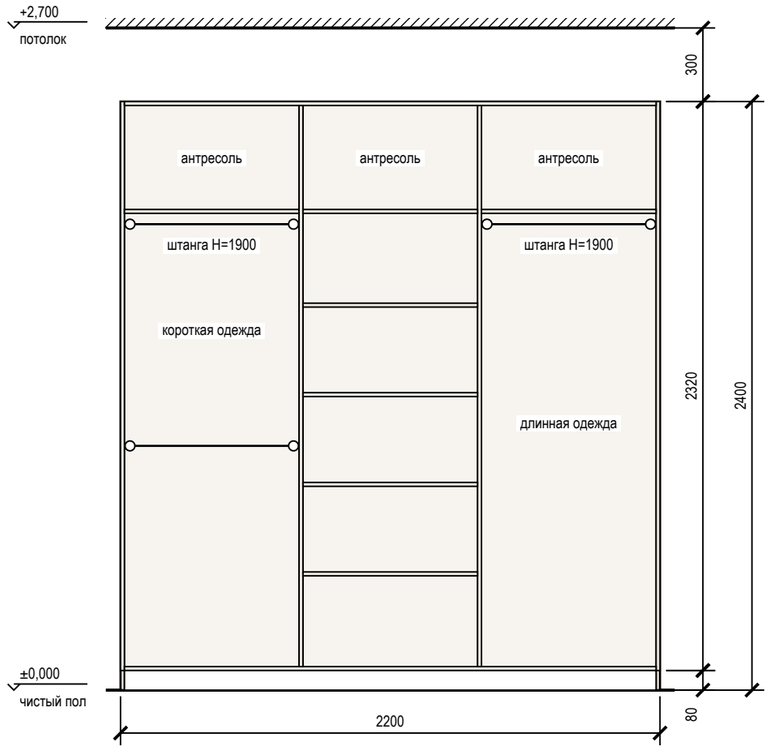


Наполнение, размеры в свету

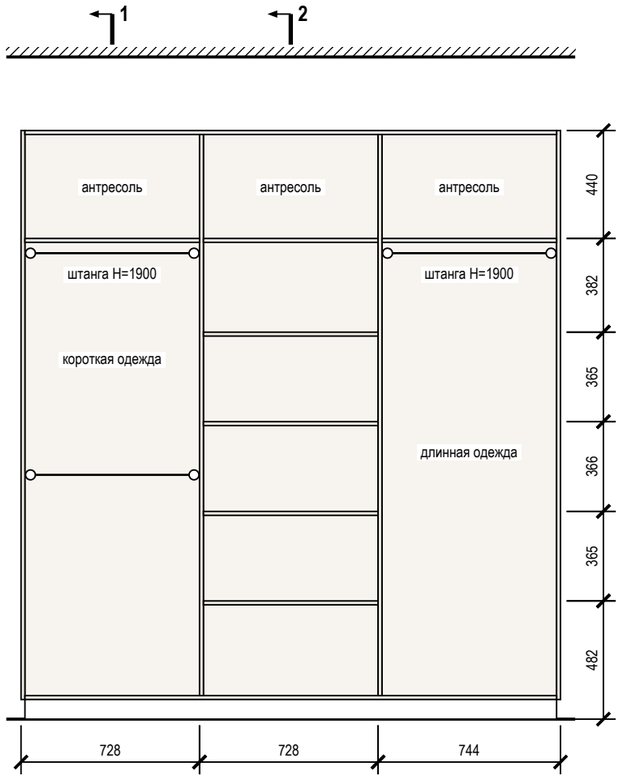

Разрез 1-1

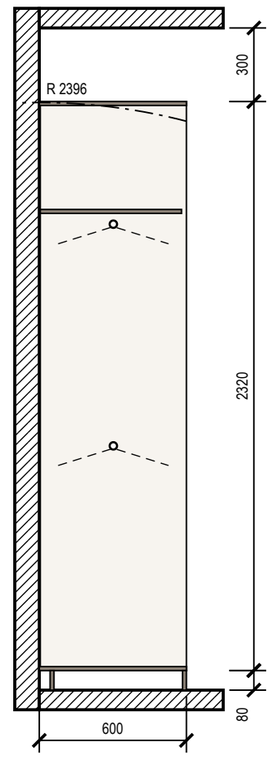

Разрез 2-2

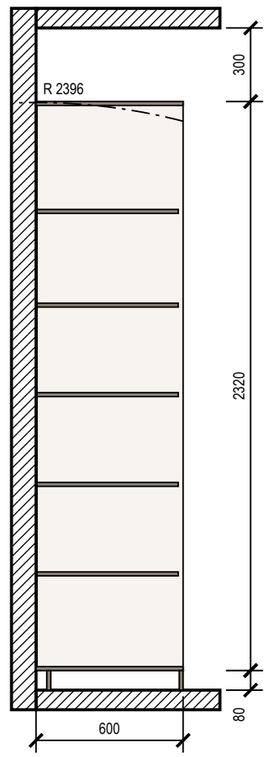

Примечания

1. Размеры — в мм по чистовой отделке; изделие 2200×600×2400 (Ш×Г×В). Перед раскроем — контрольный замер цеха после чистовой отделки стен, пола и потолка.
2. Корпус — ЛДСП 16 мм, задняя стенка ХДФ 4 мм в паз, цоколь 80 мм на регулируемых опорах; открытая система: без фасадов.
3. Кромка: скрытые торцы 0,4 мм, видимые 2 мм (ПВХ/АБС).
4. Присадка по 32-й системе — выполняет цех.
5. Зазор до потолка 300 мм.
6. Подъём корпуса: диагональ боковины без цоколя √(2320² + 600²) = 2396 мм < 2700 мм до потолка — корпус собирается лёжа, поднимается поворотом и ставится на цоколь.
7. Крепление к стене от опрокидывания: крепление к стене, 3 точки; основание стены и шаг анкеров — монтажная схема шкафов.

Условные обозначения

- корпус и полки ЛДСП (вид на стену)
- задняя стенка ХДФ
- деталь в разрезе
- штанга для плечиков (на разрезе — плечики 450 мм)
- траектория угла корпуса при подъёме в проектное положение

Допущения и предложения на листе

Основа листа: размеры сняты с растрового плана заказчика с частичными размерами: рисунок не в масштабе, помещения выровнены по подписанным размерам мебели и проходов; контрольный обмер не выполнен (К-1); высота потолка 2700 мм принята: на плане заказчика её нет (К-2); толщины стен 300 / 120 мм приняты по плану заказчика, не замерены (К-1); разрешённая мощность 15 кВт принята по типовым ТУ для квартиры, ТУ заказчиком не переданы (К-4); подрайон климата не задан — принят не северный (жилые от 2,5 м) (К-6). См. лист открытых вопросов (лист 6, записи К-1, К-2, К-4, К-6).

1000 мм · печать 1:1

Изм.	Кол.уч	Лист	№ док.	Подп.	Дата
Разраб.		Кырлан А.С.			04.11.26
Пров.					
ГИП					
Н. контр.					
Утв.					

ГД-2026-008-АИ

Квартира с кабинетом

Общая площадь 127,29* м² · * размеры со скана, не замерены (реестр — л. 6–8, К-1)

Дизайн-проект интерьера	Стадия	Лист	Листов
	РП	70	131

Система хранения Г1

М 1:25

Кырлан Александр Сергеевич


выпуск 04.11.2026 № 4177cbe7a3 · стр. 78 из 166

Система хранения Г2


Гардеробная-постирочная (пом. 2) · вид из помещения · размеры в мм, отметки в м

ПРЕДВАРИТЕЛЬНО · не для производства работ · открыто пунктов: 13 (реестр — л. 6–8)


Общий вид

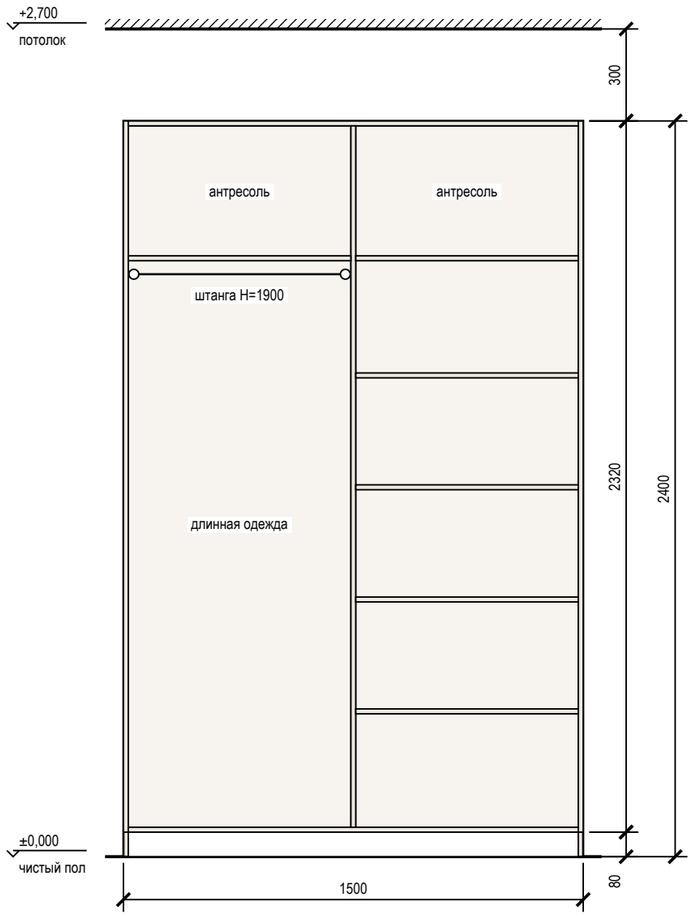


Наполнение, размеры в свету

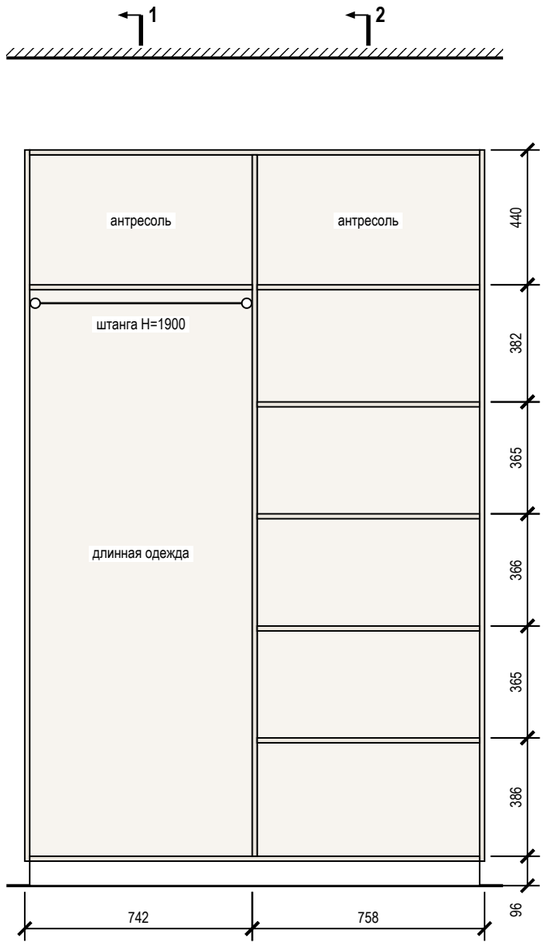

Разрез 1-1

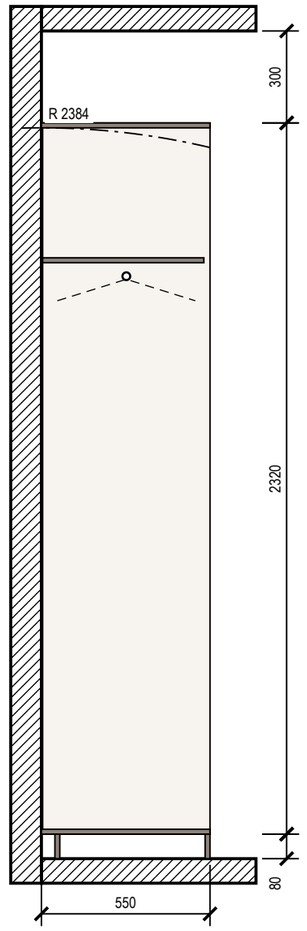

Разрез 2-2

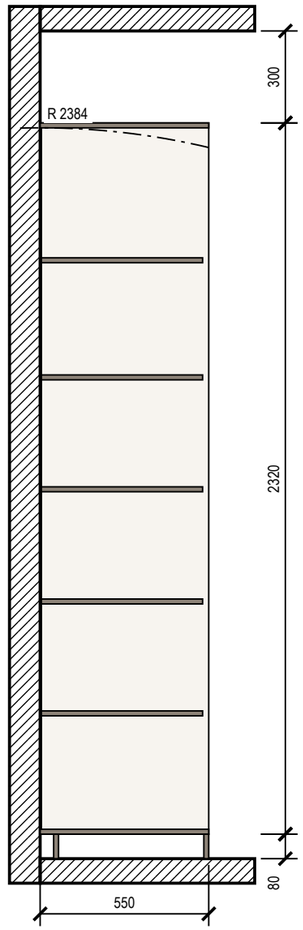

Примечания

1. Размеры — в мм по чистовой отделке; изделие 1500×550×2400 (Ш×Г×В). Перед раскроем — контрольный замер цеха после чистовой отделки стен, пола и потолка.
2. Корпус — ЛДСП 16 мм, задняя стенка ХДФ 4 мм в паз, цоколь 80 мм на регулируемых опорах; открытая система: без фасадов.
3. Кромка: скрытые торцы 0,4 мм, видимые 2 мм (ПВХ/АБС).
4. Присадка по 32-й системе — выполняет цех.
5. Зазор до потолка 300 мм.
6. Подъём корпуса: диагональ боковины без цоколя √(2320² + 550²) = 2384 мм < 2700 мм до потолка — корпус собирается лёжа, поднимается поворотом и ставится на цоколь.
7. Крепление к стене от опрокидывания: крепление к стене, 3 точки; основание стены и шаг анкеров — монтажная схема шкафов.

Условные обозначения

- корпус и полки ЛДСП (вид на стену)
- задняя стенка ХДФ
- деталь в разрезе
- штанга для плечиков (на разрезе — плечики 450 мм)
- траектория угла корпуса при подъёме в проектное положение

Допущения и предложения на листе

Основа листа: размеры сняты с растрового плана заказчика с частичными размерами: рисунок не в масштабе, помещения выровнены по подписанным размерам мебели и проходов; контрольный обмер не выполнен (К-1); высота потолка 2700 мм принята: на плане заказчика её нет (К-2); толщины стен 300 / 120 мм приняты по плану заказчика, не замерены (К-1); разрешённая мощность 15 кВт принята по типовым ТУ для квартиры, ТУ заказчиком не переданы (К-4); подрайон климата не задан — принят не северный (жилые от 2,5 м) (К-6).
См. лист открытых вопросов (лист 6, записи К-1, К-2, К-4, К-6).

1000 мм · печать 1:1

Изм.	Кол.уч	Лист	№ док.	Подп.	Дата
Разраб.		Кырлан А.С.			04.11.26
Пров.					
ГИП					
Н. контр.					
Утв.					

ГД-2026-008-АИ

Квартира с кабинетом

Общая площадь 127,29* м² · * размеры со скана, не замерены (реестр — л. 6–8, К-1)

Дизайн-проект интерьера

Стадия	Лист	Листов
РП	71	131

Система хранения Г2

М 1:20

Кырлан Александр Сергеевич


выпуск 04.11.2026 № 4177cbe7a3 · стр. 79 из 166

Шкаф распашной Кб1


Кабинет (пом. 3) · вид из помещения · размеры в мм, отметки в м

ПРЕДВАРИТЕЛЬНО · не для производства работ · открыто пунктов: 13 (реестр — л. 6–8)


Вид с фасадами

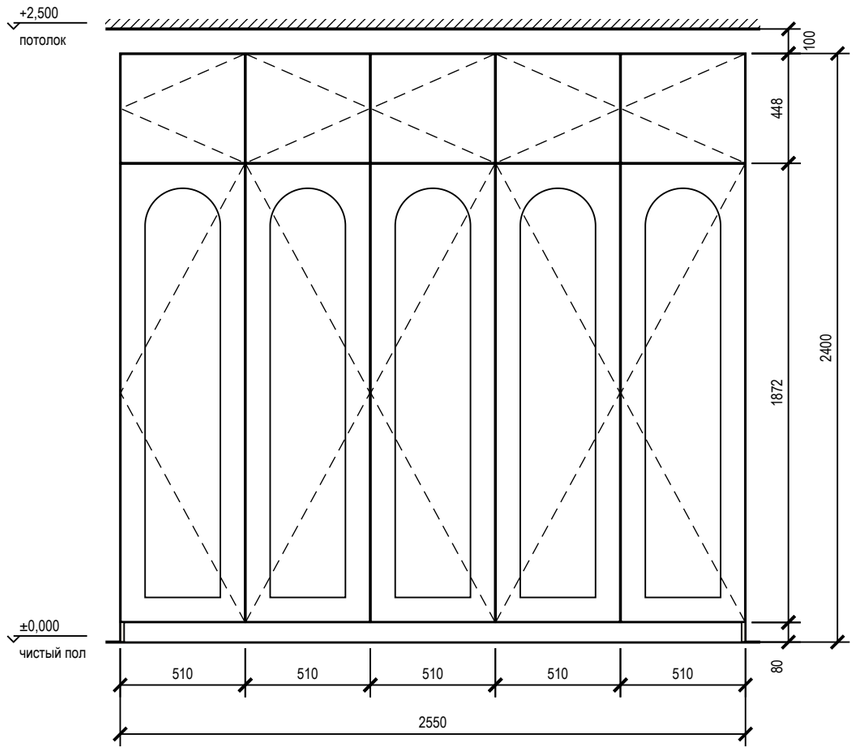


Вид без фасадов

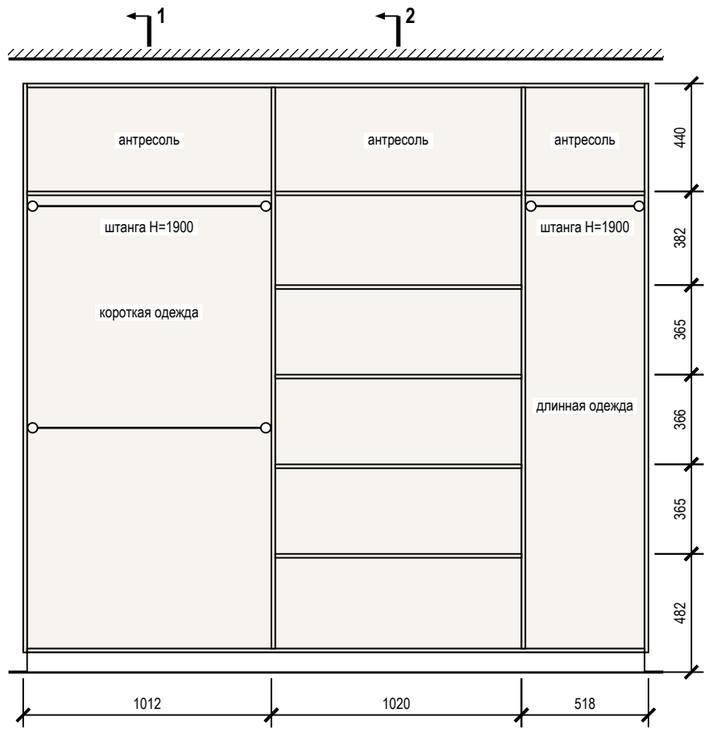

Разрез 1-1

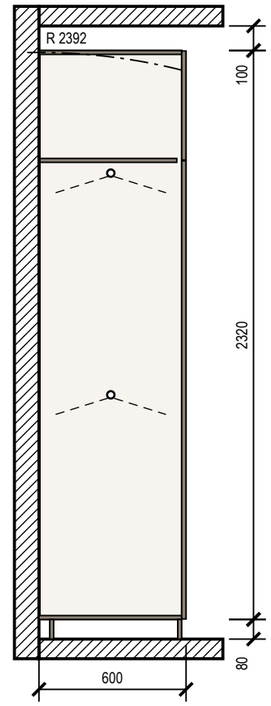

Разрез 2-2

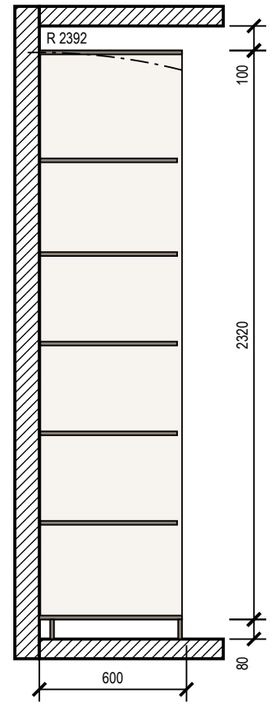

Примечания

1. Размеры — в мм по чистовой отделке; изделие 2550×600×2400 (Ш×Г×В). Перед раскроем — контрольный замер цеха после чистовой отделки стен, пола и потолка.
2. Корпус — ЛДСП 16 мм, задняя стенка ХДФ 4 мм в паз, цоколь 80 мм на регулируемых опорах; фасады накладные — МДФ 18 мм, эмаль матовая; арочная фрезеровка филёнки (полукруглый верх, поле 100 мм); цвет — по колерной карте; петли с доводчиком: фасад 1869 мм — 4 петли, фасад 445 мм — 2 петли.
3. Кромка: скрытые торцы 0,4 мм, видимые 2 мм (ПВХ/АБС).
4. Номинальные зазоры: между фасадами 3 мм, фасад — стена и фасад — потолок не менее 3 мм, фасад ящика — стойка 2 мм.
5. Присадка по 32-й системе — выполняет цех.
6. Зазор до потолка 100 мм — закрыть планкой в цвет корпуса при монтаже.
7. Подъём корпуса: диагональ боковины без цоколя √(2320² + 582²) = 2392 мм < 2500 мм до потолка — корпус собирается лёжа, поднимается поворотом и ставится на цоколь.
8. Крепление к стене от опрокидывания — уголки 2 шт. к несущему основанию (монтажная схема шкафов).

Условные обозначения

- фасад распашной: линии сходятся к стороне петель
- корпус и полки ЛДСП (вид на стену)
- задняя стенка ХДФ
- деталь в разрезе
- арочная фрезеровка филёнки фасада
- штанга для плечиков (на разрезе — плечики 450 мм)
- траектория угла корпуса при подъёме в проектное положение

Допущения и предложения на листе

Основа листа: размеры сняты с растрового плана заказчика с частичными размерами: рисунок не в масштабе, помещения выровнены по подписанным размерам мебели и проходов; контрольный обмер не выполнен (К-1); высота потолка 2700 мм принята: на плане заказчика её нет (К-2); толщины стен 300 / 120 мм приняты по плану заказчика, не замерены (К-1); разрешённая мощность 15 кВт принята по типовым ТУ для квартиры, ТУ заказчиком не переданы (К-4); подрайон климата не задан — принят не северный (жилые от 2,5 м) (К-6).
См. лист открытых вопросов (лист 6, записи К-1, К-2, К-4, К-6).

1000 мм · печать 1:1

Изм.	Кол.уч	Лист	№ док.	Подп.	Дата
Разраб.		Кырлан А.С.			04.11.26
Пров.					
ГИП					
Н. контр.					
Утв.					

ГД-2026-008-АИ

Квартира с кабинетом

Общая площадь 127,29* м² · * размеры со скана, не замерены (реестр — л. 6–8, К-1)

Дизайн-проект интерьера

Стадия	Лист	Листов
РП	72	131

Шкаф распашной Кб1

М 1:25

Кырлан Александр Сергеевич


выпуск 04.11.2026 № 4177cbe7a3 · стр. 80 из 166

ТВ-стена Кх12


Кухня-гостиная (пом. 4) · вид из помещения · размеры в мм, отметки в м

ПРЕДВАРИТЕЛЬНО · не для производства работ · открыто пунктов: 13 (реестр — л. 6–8)


Вид с облицовкой

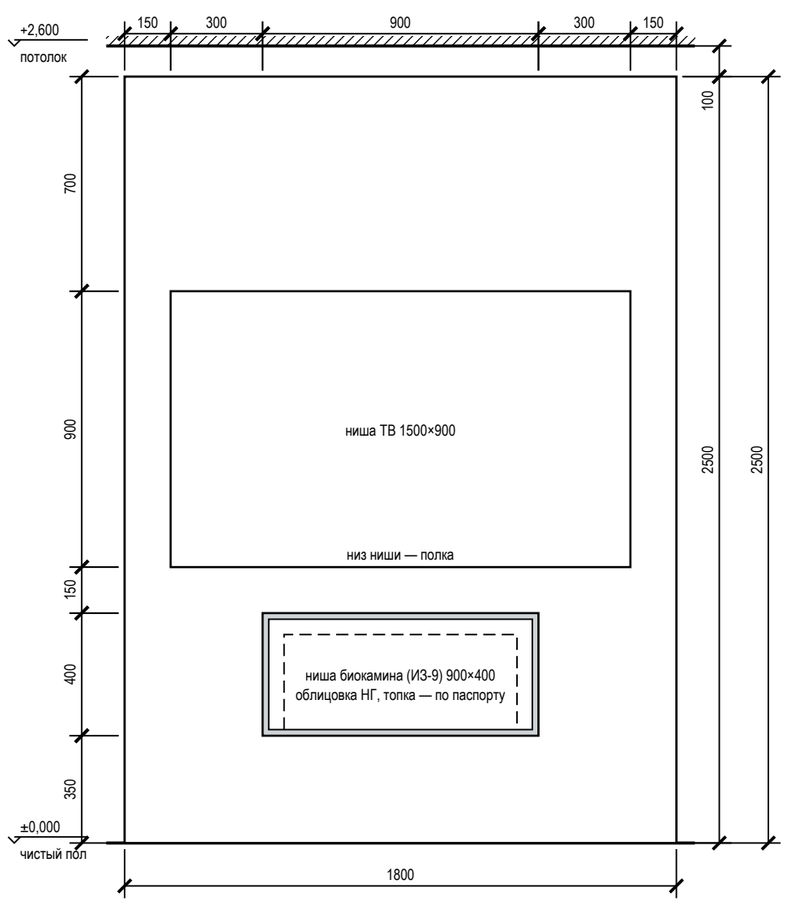

Каркас (без облицовки)

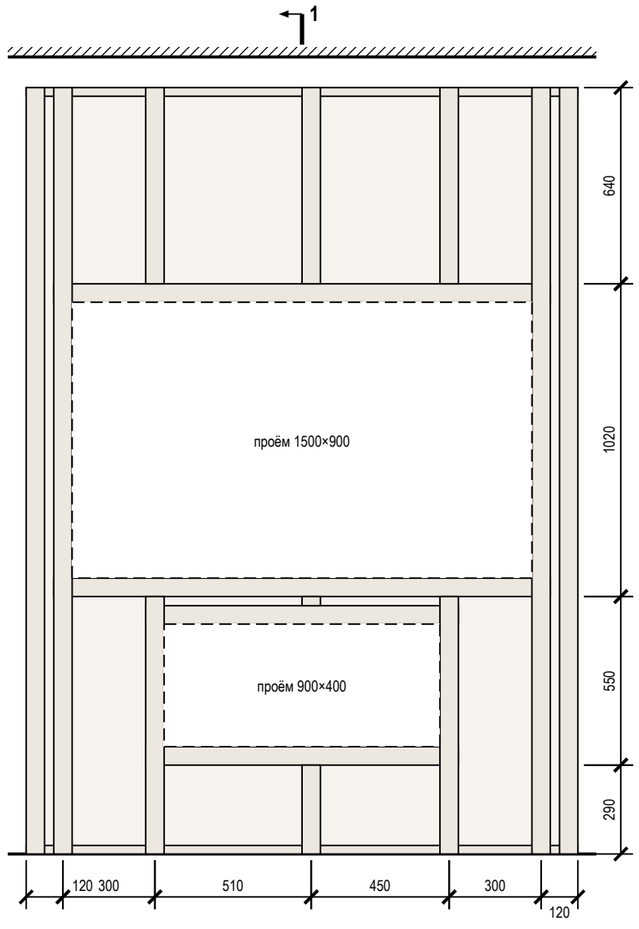

Разрез 1-1 по нишам ТВ и биокамина

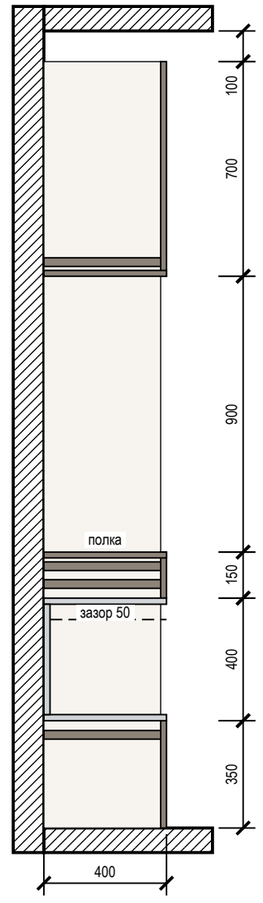

Примечания

1. Размеры — в мм по чистовой отделке; изделие 1800×400×2500 (Ш×Г×В). Встроенная ТВ-стена, не корпусная мебель: отделений, штанг, ящиков и антресолей нет. Перед изготовлением контрольный замер стены после штукатурки и пола.
2. Каркас — оцинкованный профиль ПП 60×27 / ПН 28×27 (НГ), на стене Б; стойки по краям изделия и ниш, промежуточные с шагом не более 600 мм, ригели над и под нишами; облицовка панели МДФ 19 мм с волнистым рельефом, эмаль матовая; цвет — по колерной карте. Собирается на месте у стены, траектории подъёма нет.
3. Ниша ТВ 1500×900, низ +900, глубина 400: низ ниши — полка под приставку, электроточки ТВ-зоны — внутри ниши за телевизором, кабель-канал в каркасе.
4. Ниша биокамина (ИЗ-9) 900×400, низ +350: облицовка — сталь листовая 2 мм / камень натуральный, негорючие (НГ, ГОСТ 30244), 20 мм; зазоры до топки над ней 50 мм, по бокам 50 мм — до выбора модели; окончательно — по паспорту биокамина (ИЗ-9). Каркас вокруг ниши — металлический профиль (НГ), ЛДСП, МДФ и дерево в нише и в зазорах не применять.
5. ТВ над топкой: от верха ниши биокамина (ИЗ-9) (+750) до низа ниши ТВ (+900) — 150 мм; нагрев телевизора и приставки над топкой — расстояние по паспортам обеих моделей (К-20); до выбора моделей нишу ТВ не изготавливать.
6. Крепление к стене: стойки и направляющие — анкерами к основанию стены; основание стены и шаг анкеров — монтажная схема.

Условные обозначения

- облицовка панелями (вид)
- каркас: стойки и ригели из профиля
- облицовка ниши камина негорючая (НГ)
- топка биокамина — по паспорту, в пределах зазоров
- деталь в разрезе

Допущения и предложения на листе

Основа листа: размеры сняты с растрового плана заказчика с частичными размерами: рисунок не в масштабе, помещения выровнены по подписанным размерам мебели и проходов; контрольный обмер не выполнен (К-1); высота потолка 2700 мм принята: на плане заказчика её нет (К-2); толщины стен 300 / 120 мм приняты по плану заказчика, не замерены (К-1); разрешённая мощность 15 кВт принята по типовым ТУ для квартиры, ТУ заказчиком не переданы (К-4); подрайон климата не задан — принят не северный (жилые от 2,5 м) (К-6).
Открытые вопросы и конфликты по листу: К-20.
См. лист открытых вопросов (лист 6, записи К-1, К-2, К-4, К-6; лист 7, запись К-20).

1000 мм · печать 1:1

Изм.	Кол.уч	Лист	№ док.	Подп.	Дата
Разраб.		Кырлан А.С.			04.11.26
Пров.					
ГИП					
Н. контр.					
Утв.					

ГД-2026-008-АИ

Квартира с кабинетом

Общая площадь 127,29* м² · * размеры со скана, не замерены (реестр — л. 6–8, К-1)

Дизайн-проект интерьера

Стадия	Лист	Листов
РП	73	131

ТВ-стена Кх12

М 1:20

Кырлан Александр Сергеевич


выпуск 04.11.2026 № 4177cbe7a3 · стр. 81 из 166

Шкаф распашной Кх13


Кухня-гостиная (пом. 4) · вид из помещения · размеры в мм, отметки в м

ПРЕДВАРИТЕЛЬНО · не для производства работ · открыто пунктов: 13 (реестр — л. 6–8)


Вид с фасадами

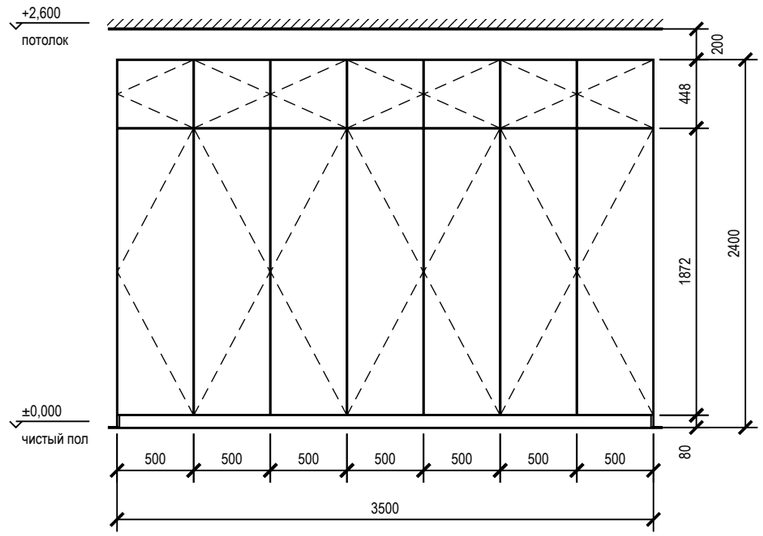


Вид без фасадов

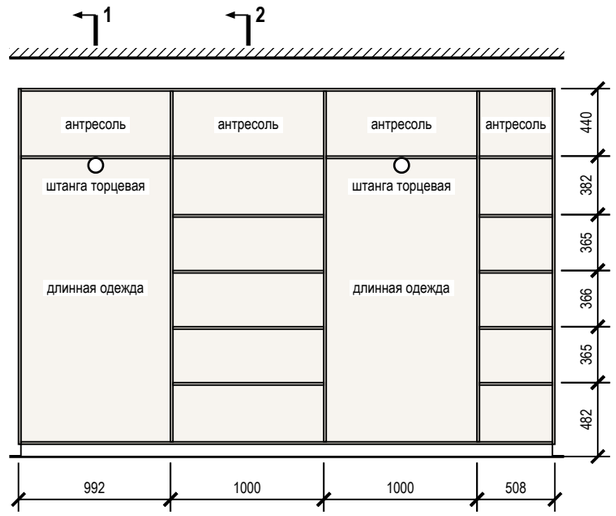

Разрез 1-1

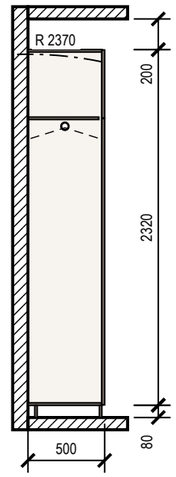

Разрез 2-2

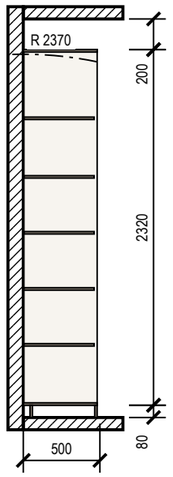

Примечания

1. Размеры — в мм по чистовой отделке; изделие 3500×500×2400 (Ш×Г×В). Перед раскроем — контрольный замер цеха после чистовой отделки стен, пола и потолка.
2. Корпус — ЛДСП 16 мм, задняя стенка ХДФ 4 мм в паз, цоколь 80 мм на регулируемых опорах; фасады накладные — МДФ 18 мм, эмаль матовая, 18 мм; цвет — по колерной карте; петли с доводчиком: фасад 1869 мм — 4 петли, фасад 445 мм — 2 петли.
3. Кромка: скрытые торцы 0,4 мм, видимые 2 мм (ПВХ/АБС).
4. Номинальные зазоры: между фасадами 3 мм, фасад — стена и фасад — потолок не менее 3 мм, фасад ящика — стойка 2 мм.
5. Присадка по 32-й системе — выполняет цех.
6. Зазор до потолка 200 мм.
7. Подъём корпуса: диагональ боковины без цоколя $\sqrt{(2320^2 + 482^2)} = 2370$ мм < 2600 мм до потолка — корпус собирается лёжа, поднимается поворотом и ставится на цоколь.
8. Крепление к стене от опрокидывания — уголки 2 шт. к несущему основанию (монтажная схема шкафов).

Условные обозначения

- фасад распашной: линии сходятся к стороне петель
- корпус и полки ЛДСП (вид на стену)
- задняя стенка ХДФ
- деталь в разрезе
- штанга для плечиков (на разрезе — плечики 450 мм)
- траектория угла корпуса при подъёме в проектное положение

Допущения и предложения на листе

Основа листа: размеры сняты с растрового плана заказчика с частичными размерами: рисунок не в масштабе, помещения выровнены по подписанным размерам мебели и проходов; контрольный обмер не выполнен (К-1); высота потолка 2700 мм принята: на плане заказчика её нет (К-2); толщины стен 300 / 120 мм приняты по плану заказчика, не замерены (К-1); разрешённая мощность 15 кВт принята по типовым ТУ для квартиры, ТУ заказчиком не переданы (К-4); подрайон климата не задан — принят не северный (жилые от 2,5 м) (К-6).
См. лист открытых вопросов (лист 6, записи К-1, К-2, К-4, К-6).

1000 мм · печать 1:1

Изм.	Кол.уч	Лист	№ док.	Подп.	Дата
Разраб.		Кырлан А.С.			04.11.26
Пров.					
ГИП					
Н. контр.					
Утв.					

ГД-2026-008-АИ

Квартира с кабинетом

Общая площадь 127,29* м² · * размеры со скана, не замерены (реестр — л. 6–8, К-1)

Дизайн-проект интерьера

Стадия	Лист	Листов
РП	74	131

Шкаф распашной Кх13

М 1:40

Кырлан Александр Сергеевич


выпуск 04.11.2026 № 4177cbe7a3 · стр. 82 из 166

Шкаф распашной Дт1


Детская (пом. 6) · вид из помещения · размеры в мм, отметки в м

ПРЕДВАРИТЕЛЬНО · не для производства работ · открыто пунктов: 13 (реестр — л. 6–8)


Вид с фасадами

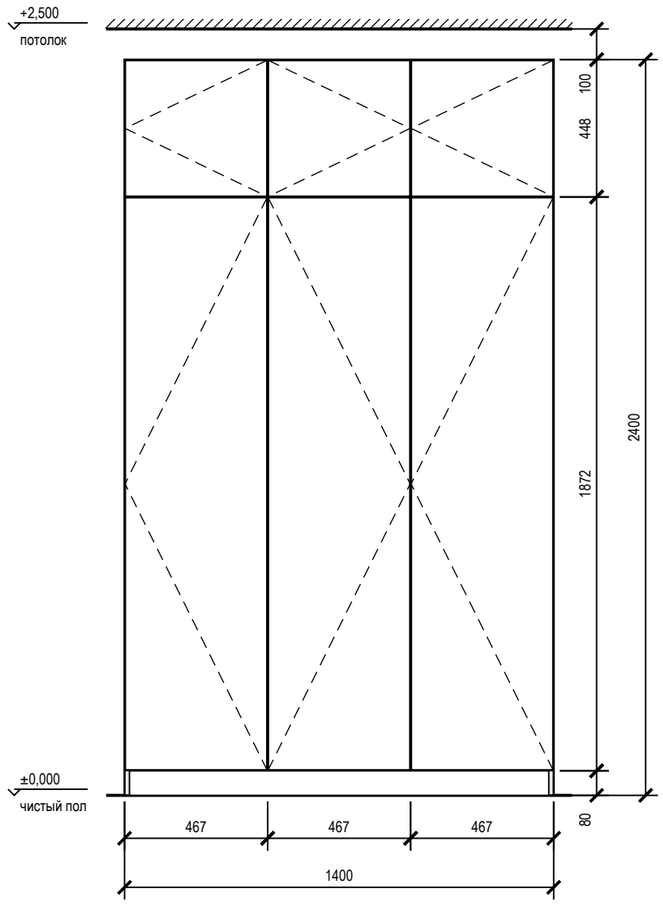


Вид без фасадов

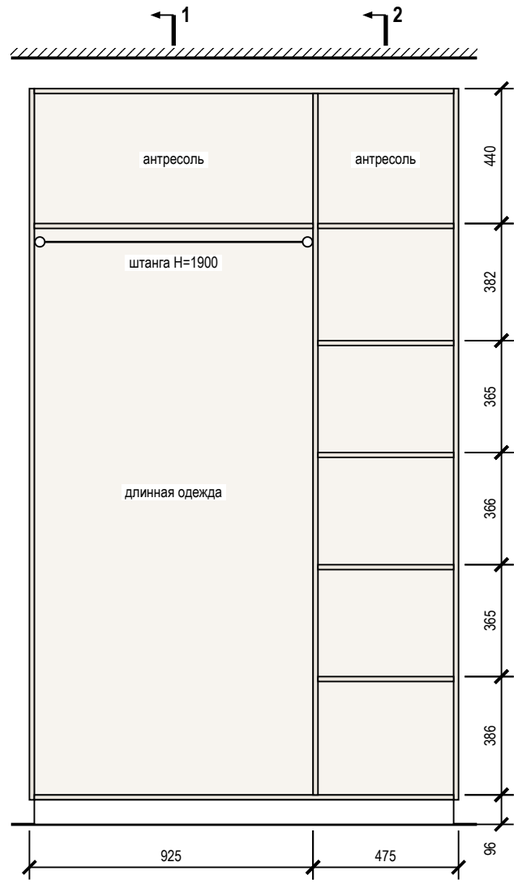

Разрез 1-1

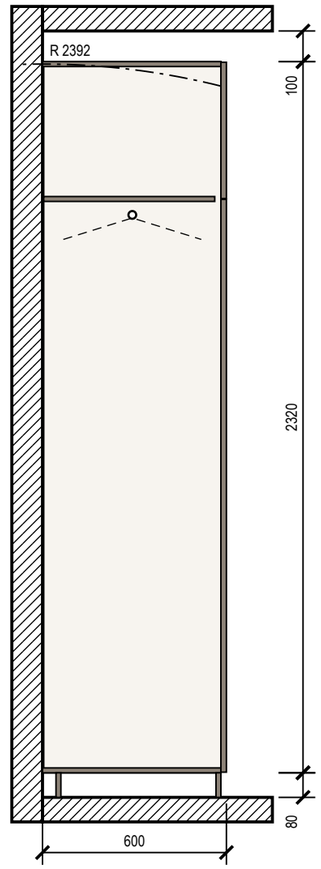

Разрез 2-2

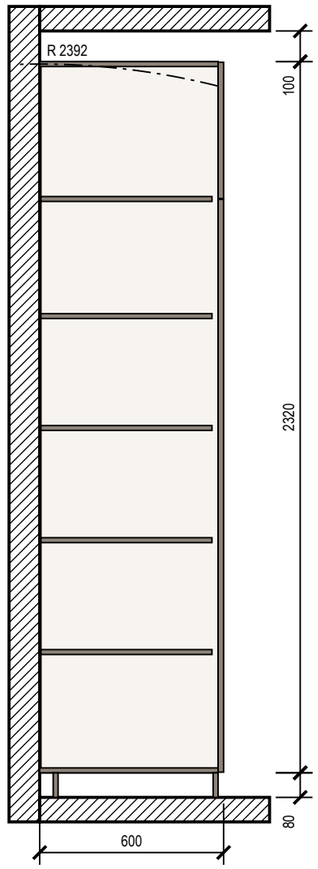

Примечания

1. Размеры — в мм по чистовой отделке; изделие 1400×600×2400 (Ш×Г×В). Перед раскроем — контрольный замер цеха после чистовой отделки стен, пола и потолка.
2. Корпус — ЛДСП 16 мм, задняя стенка ХДФ 4 мм в паз, цоколь 80 мм на регулируемых опорах; фасады накладные — МДФ 18 мм, эмаль матовая, 18 мм; цвет — по колерной карте; петли с доводчиком: фасад 1869 мм — 4 петли, фасад 445 мм — 2 петли.
3. Кромка: скрытые торцы 0,4 мм, видимые 2 мм (ПВХ/АБС).
4. Номинальные зазоры: между фасадами 3 мм, фасад — стена и фасад — потолок не менее 3 мм, фасад ящика — стойка 2 мм.
5. Присадка по 32-й системе — выполняет цех.
6. Зазор до потолка 100 мм — закрыть планкой в цвет корпуса при монтаже.
7. Подъём корпуса: диагональ боковины без цоколя √(2320² + 582²) = 2392 мм < 2500 мм до потолка — корпус собирается лёжа, поднимается поворотом и ставится на цоколь.
8. Крепление к стене от опрокидывания: крепление к стене, 2 точки; основание стены и шаг анкеров — монтажная схема шкафов.

Условные обозначения

- фасад распашной: линии сходятся к стороне петель
- корпус и полки ЛДСП (вид на стену)
- задняя стенка ХДФ
- деталь в разрезе
- штанга для плечиков (на разрезе — плечики 450 мм)
- траектория угла корпуса при подъёме в проектное положение

Допущения и предложения на листе

Основа листа: размеры сняты с растрового плана заказчика с частичными размерами: рисунок не в масштабе, помещения выровнены по подписанным размерам мебели и проходов; контрольный обмер не выполнен (К-1); высота потолка 2700 мм принята: на плане заказчика её нет (К-2); толщины стен 300 / 120 мм приняты по плану заказчика, не замерены (К-1); разрешённая мощность 15 кВт принята по типовым ТУ для квартиры, ТУ заказчиком не переданы (К-4); подрайон климата не задан — принят не северный (жилые от 2,5 м) (К-6).
См. лист открытых вопросов (лист 6, записи К-1, К-2, К-4, К-6).

1000 мм · печать 1:1

Изм.	Кол.уч	Лист	№ док.	Подп.	Дата
Разраб.		Кырлан А.С.			04.11.26
Пров.					
ГИП					
Н. контр.					
Утв.					

ГД-2026-008-АИ

Квартира с кабинетом

Общая площадь 127,29* м² · * размеры со скана, не замерены (реестр — л. 6–8, К-1)

Дизайн-проект интерьера

Стадия	Лист	Листов
РП	75	131

Шкаф распашной Дт1

М 1:20

Кырлан Александр Сергеевич


выпуск 04.11.2026 № 4177cbe7a3 · стр. 83 из 166

Тумба под раковину Вн1


Ванная (пом. 7) · вид из помещения · размеры в мм, отметки в м

ПРЕДВАРИТЕЛЬНО · не для производства работ · открыто пунктов: 13 (реестр — л. 6–8)


Вид с фасадами

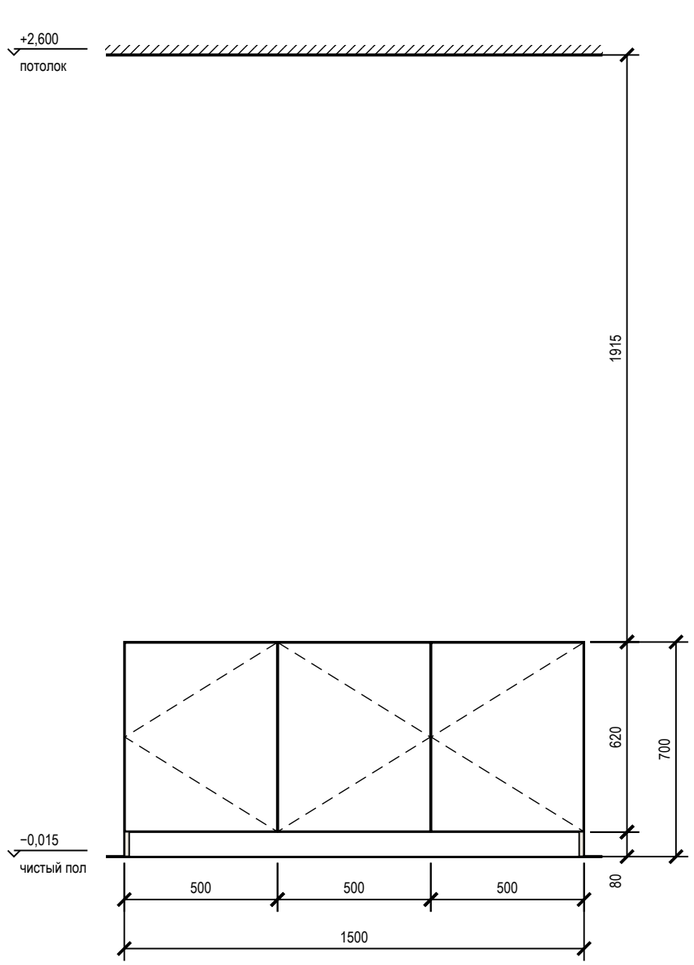

Вид без фасадов

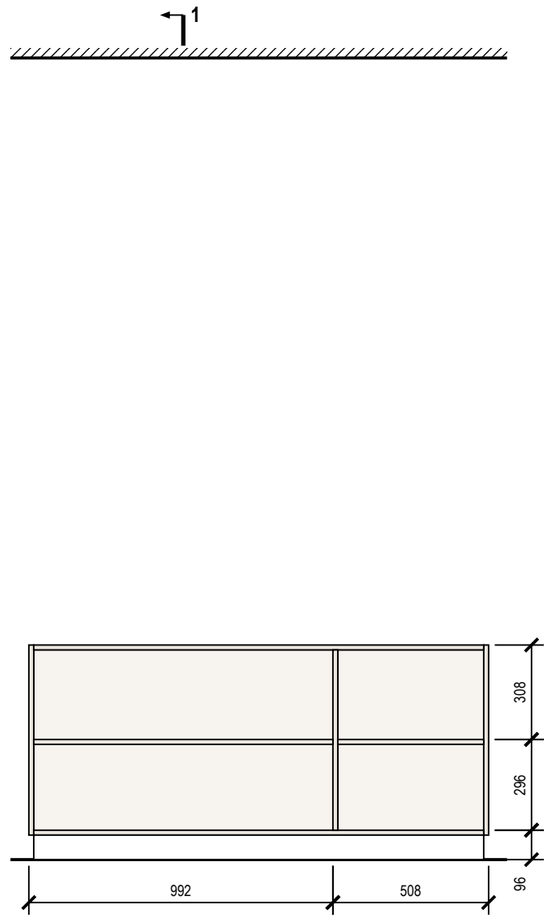

Разрез 1-1

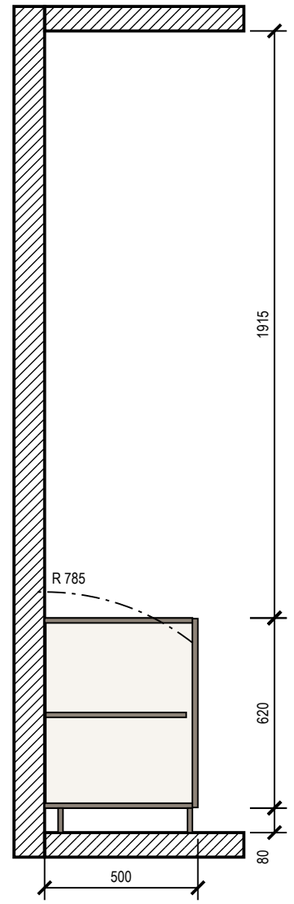

Примечания

1. Размеры — в мм по чистовой отделке; изделие 1500×500×700 (Ш×Г×В). Перед раскроем — контрольный замер цеха после чистовой отделки стен, пола и потолка.
2. Корпус — ЛДСП 16 мм, задняя стенка ХДФ 4 мм в паз, цоколь 80 мм на регулируемых опорах; фасады накладные — МДФ 18 мм, эмаль матовая, 18 мм; цвет — по колерной карте; петли с доводчиком: фасад 616 мм — 2 петли.
3. Кромка: скрытые торцы 0,4 мм, видимые 2 мм (ПВХ/АБС).
4. Номинальные зазоры: между фасадами 3 мм, фасад — стена и фасад — потолок не менее 3 мм, фасад ящика — стойка 2 мм.
5. Присадка по 32-й системе — выполняет цех.
6. Зазор до потолка 1915 мм.
7. Подъём корпуса: диагональ боковины без цоколя √(620² + 482²) = 785 мм < 2615 мм до потолка — корпус собирается лёжа, поднимается поворотом и ставится на цоколь.
8. Крепление к стене от опрокидывания: крепление к стене, 2 точки; основание стены и шаг анкеров — монтажная схема шкафов.

Условные обозначения

- фасад распашной: линии сходятся к стороне петель
- корпус и полки ЛДСП (вид на стену)
- задняя стенка ХДФ
- деталь в разрезе
- штанга для плечиков (на разрезе — плечики 450 мм)
- траектория угла корпуса при подъёме в проектное положение

Допущения и предложения на листе

Основа листа: размеры сняты с растрового плана заказчика с частичными размерами: рисунок не в масштабе, помещения выровнены по подписанным размерам мебели и проходов; контрольный обмер не выполнен (К-1); высота потолка 2700 мм принята: на плане заказчика её нет (К-2); толщины стен 300 / 120 мм приняты по плану заказчика, не замерены (К-1); разрешённая мощность 15 кВт принята по типовым ТУ для квартиры, ТУ заказчиком не переданы (К-4); подрайон климата не задан — принят не северный (жилые от 2,5 м) (К-6).
См. лист открытых вопросов (лист 6, записи К-1, К-2, К-4, К-6).

1000 мм · печать 1:1

Изм.	Кол.уч	Лист	№ док.	Подп.	Дата
Разраб.		Кырлан А.С.			04.11.26
Пров.					
ГИП					
Н. контр.					
Утв.					

ГД-2026-008-АИ

Квартира с кабинетом

Общая площадь 127,29* м² · * размеры со скана, не замерены (реестр — л. 6–8, К-1)

Дизайн-проект интерьера

Стадия	Лист	Листов
РП	76	131

Тумба под раковину Вн1

М 1:20

Кырлан Александр Сергеевич


выпуск 04.11.2026 № 4177cbe7a3 · стр. 84 из 166

Шкаф-купе Пх1


Прихожая (пом. 8) · вид из помещения · размеры в мм, отметки в м

ПРЕДВАРИТЕЛЬНО · не для производства работ · открыто пунктов: 13 (реестр — л. 6–8)


Вид с фасадами

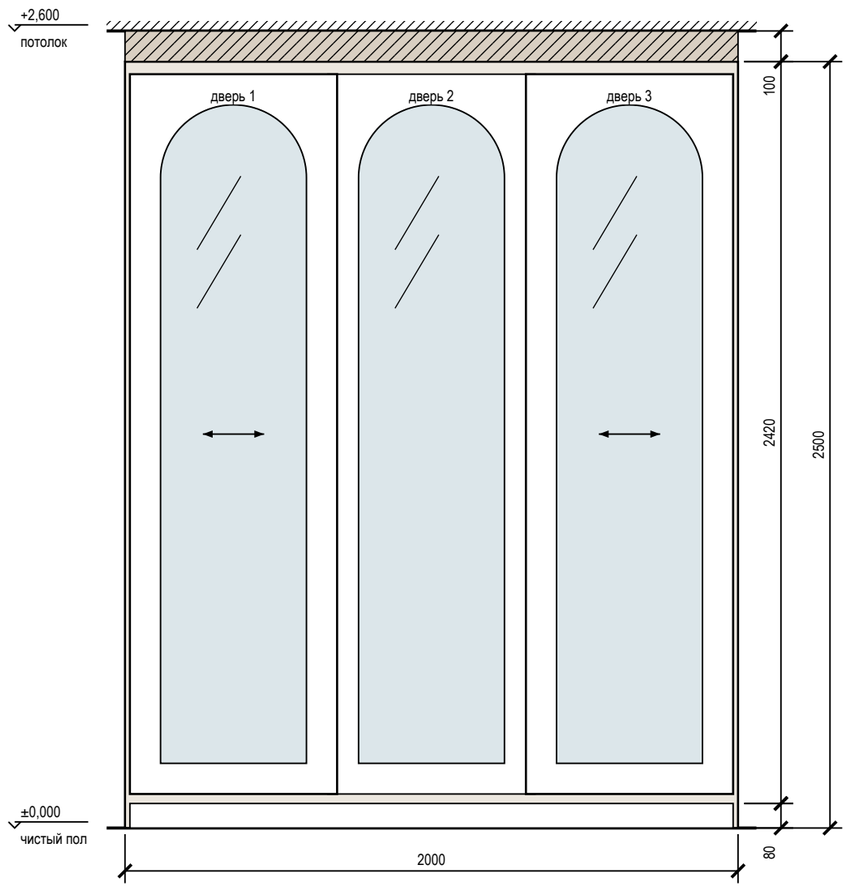


Вид без фасадов

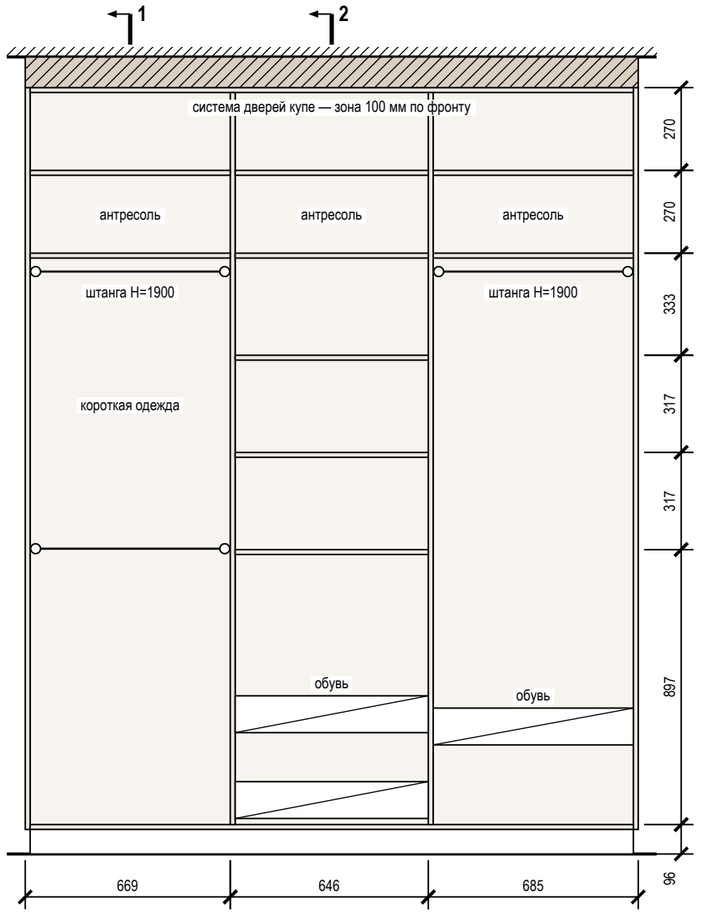

Разрез 1-1

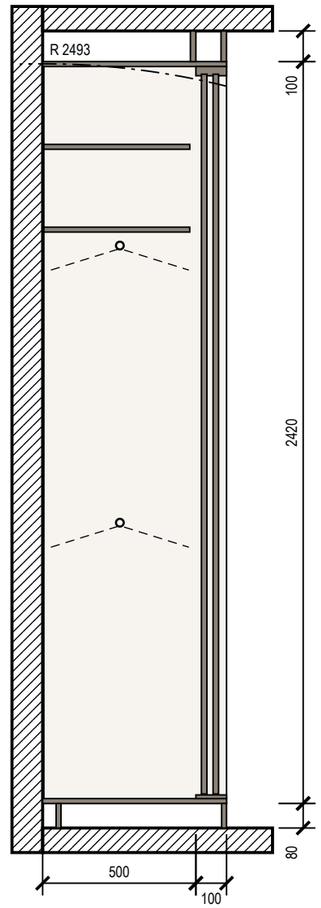

Разрез 2-2

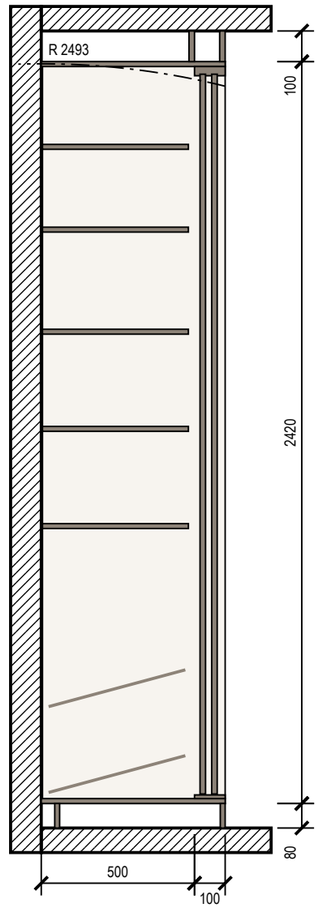

Примечания

1. Размеры — в мм по чистовой отделке; изделие 2000×600×2500 (Ш×Г×В). Перед раскроем — контрольный замер цеха после чистовой отделки стен, пола и потолка.
2. Корпус — ЛДСП 16 мм, задняя стенка ХДФ 4 мм в паз, цоколь 80 мм на регулируемых опорах; двери купе — МДФ 10 мм, эмаль матовая в профиле: алюминий, латунь матовая; вставка зеркало серебро 4 мм, плёнка безопасности, арочная (полукруглый верх, поле 100 мм); нахлёст 30 мм, ширина двери 676 мм, высота — проём минус 40 мм; цвет — по колерной карте.
3. Кромка: скрытые торцы 0,4 мм, видимые 2 мм (ПВХ/АБС).
4. Номинальные зазоры: дверь купе — боковина 3 мм, фасад ящика — стойка 2 мм; ящики внутри купе — с накладкой 30 мм на стойке со стороны нахлёста дверей.
5. Присадка по 32-й системе — выполняет цех.
6. Компенсатор 100 мм — короб из ЛДСП по фронту и торцам, подгоняется к потолку при монтаже (припуск 20 мм), крепится к корпусу и к потолку.
7. Подъём корпуса: диагональ боковины без цоколя √(2420² + 600²) = 2493 мм < 2600 мм до потолка — корпус собирается лёжа, поднимается поворотом и ставится на цоколь.
8. Крепление к стене от опрокидывания — уголки 2 шт. к несущему основанию (монтажная схема шкафов).

Условные обозначения

- дверь купе, стрелка — направление движения
- корпус и полки ЛДСП (вид на стену)
- задняя стенка ХДФ
- деталь в разрезе
- компенсатор — короб до потолка
- зеркальная вставка фасада (арочная)
- штанга для плечиков (на разрезе — плечики 450 мм)
- траектория угла корпуса при подъёме в проектное положение

Допущения и предложения на листе

Основа листа: размеры сняты с растрового плана заказчика с частичными размерами: рисунок не в масштабе, помещения выровнены по подписанным размерам мебели и проходов; контрольный обмер не выполнен (К-1); высота потолка 2700 мм принята: на плане заказчика её нет (К-2); толщины стен 300 / 120 мм приняты по плану заказчика, не замерены (К-1); разрешённая мощность 15 кВт принята по типовым ТУ для квартиры, ТУ заказчиком не переданы (К-4); подрайон климата не задан — принят не северный (жилые от 2,5 м) (К-6).
См. лист открытых вопросов (лист 6, записи К-1, К-2, К-4, К-6).

1000 мм · печать 1:1

Изм.	Кол.уч	Лист	№ док.	Подп.	Дата
Разраб.		Кырлан А.С.			04.11.26
Пров.					
ГИП					
Н. контр.					
Утв.					

ГД-2026-008-АИ

Квартира с кабинетом

Общая площадь 127,29* м² · * размеры со скана, не замерены (реестр — л. 6–8, К-1)

Дизайн-проект интерьера

Стадия	Лист	Листов
РП	77	131

Шкаф-купе Пх1

М 1:20


Кырлан Александр Сергеевич

Кухня (пом. 4). Развёртка гарнитура


Кухня-гостиная (пом. 4) · стена А · вид из помещения · размеры в мм, отметки в м

ПРЕДВАРИТЕЛЬНО · не для производства работ · открыто пунктов: 13 (реестр — л. 6–8)

Вид с фасадами

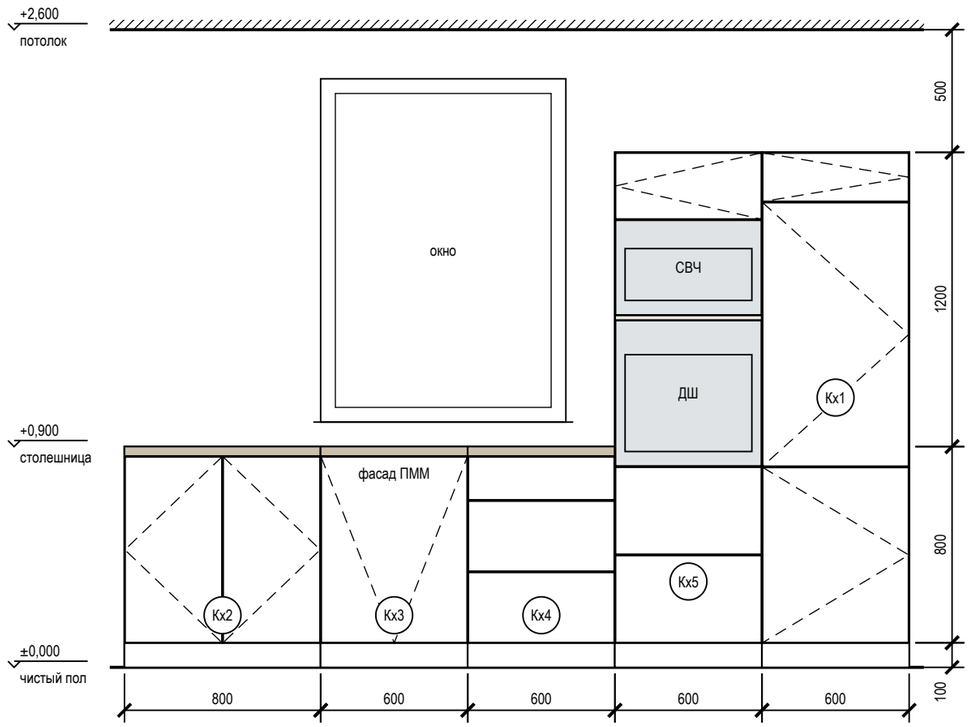

Вид без фасадов (наполнение, выводы)

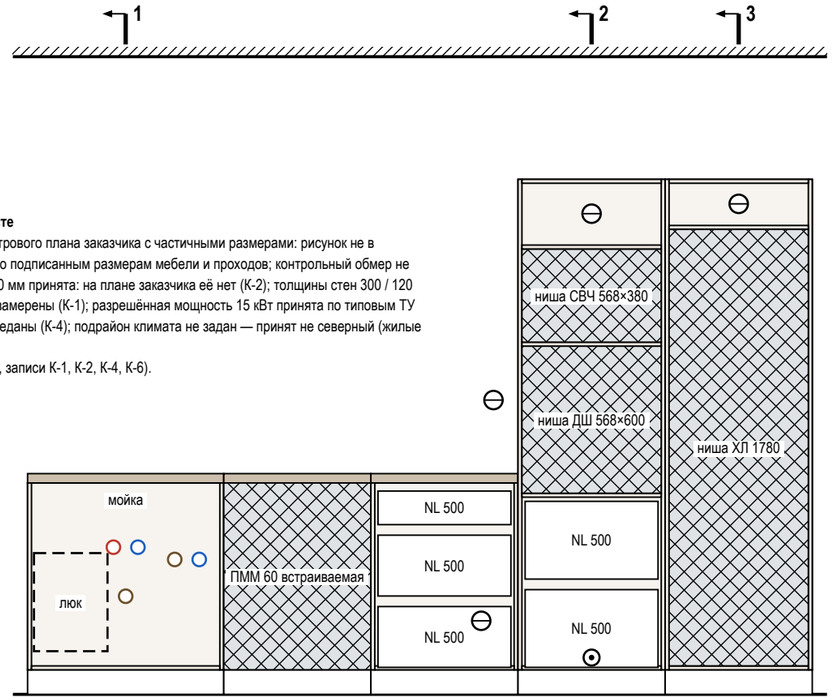

Допущения и предложения на листе


Основа листа: размеры сняты с растрового плана заказчика с частичными размерами: рисунок не в масштабе, помещения выровнены по подписанным размерам мебели и проходов; контрольный обмер не выполнен (К-1); высота потолка 2700 мм принята: на плане заказчика её нет (К-2); толщины стен 300 / 120 мм приняты по плану заказчика, не замерены (К-1); разрешённая мощность 15 кВт принята по типовым ТУ для квартиры, ТУ заказчиком не переданы (К-4); подрайон климата не задан — принят не северный (жилые от 2,5 м) (К-6).

См. лист открытых вопросов (лист 6, записи К-1, К-2, К-4, К-6).

Разрез 1-1

Разрез 2-2

Разрез 3-3

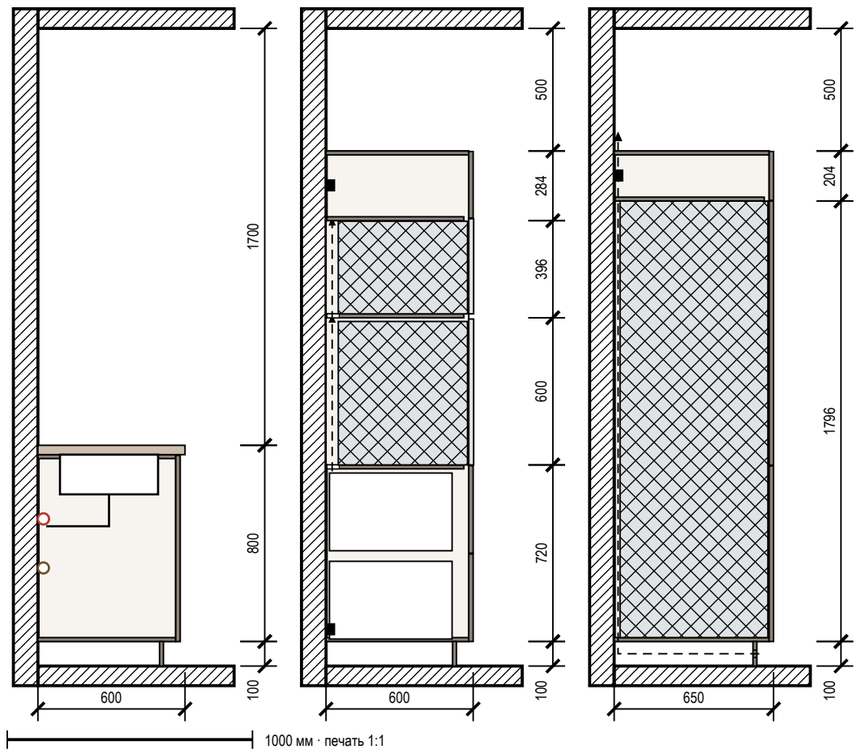

Условные обозначения

- фасад распашной: линии сходятся к стороне петель
- фасад ящика, карго
- встраиваемая техника
- столешница
- доборная планка
- деталь в разрезе
- К1 — марка изделия или модуля (на схеме расположения под ней — лист изделия)
- розетка на стене
- вывод кабеля к технике
- В1 — вывод воды В1 / Т3, канализации К1

Примечания

1. Размеры — в мм по чистовой отделке, вид из помещения; марки — как на плане расстановки. Перед раскроем — контрольный замер цеха после фартука и пола.
2. Корпуса — ЛДСП 16 мм, задняя стенка ХДФ 4 мм; фасады — МДФ, эмаль матовая 18 мм, цвет по колерной карте; столешница 38 мм, свес 20 мм; цоколь 100 мм.
3. Кромка: скрытые торцы 0,4 мм, видимые 2 мм. Номинальные зазоры: между фасадами 3 мм, фасад — столешница 3 мм, фасад — стена не менее 3 мм.
4. Ящики полного выдвижения и петли — с доводчиком; присадка по 32-й системе — выполняет цех.
5. Ниши техники (холодильник — ориентир 1780 мм) — по монтажным схемам выбранных моделей: решётка в цоколе и канал за пеналом холодильника, зазор за духовым шкафом, фасад ПММ на двери машины.
6. Кх5: ниша ДШ 568×600×550 (низ +820), ниша СВЧ 568×380×550 (низ +1436) — по габаритам ведомости техники (прибор 60 см, модель не выбрана); вентиляция: задняя стенка в зоне ниш не ставится, зазор 50 мм до стены, щель 50 мм в полке под каждой нишей у задней стенки.
7. Кх2: сервисный люк к стоякам Ст К1-3 (кухня), Ст В1-3 — съёмная панель 300×400 мм в задней стенке на саморезах (по виду без фасадов, штриховой контур «люк»), доступ через фасад модуля; короб стояков за модулем — с ревизией напротив люка (лист ВК).

Изм.	Кол.уч	Лист	№ док.	Подп.	Дата
Разраб.		Кырлан А.С.			04.11.26
Пров.					
ГИП					
Н. контр.					
Утв.					

ГД-2026-008-АИ

Квартира с кабинетом

Общая площадь 127,29* м² · * размеры со скана, не замерены (реестр — л. 6–8, К-1)

Дизайн-проект интерьера

Стадия	Лист	Листов
РП	78	131

Кухня (пом. 4). Развёртка гарнитура

М 1:25

Кырлан Александр Сергеевич


выпуск 04.11.2026 № 4177cbe7a3 · стр. 86 из 166

Кухня (пом. 4). Монтажная схема


Кухня-гостиная (пом. 4) · стена А · размеры в мм от чистых поверхностей, высоты — от чистого пола

ПРЕДВАРИТЕЛЬНО · не для производства работ · открыто пунктов: 13 (реестр — л. 6–8)

Привязка выводов и крепление модулей

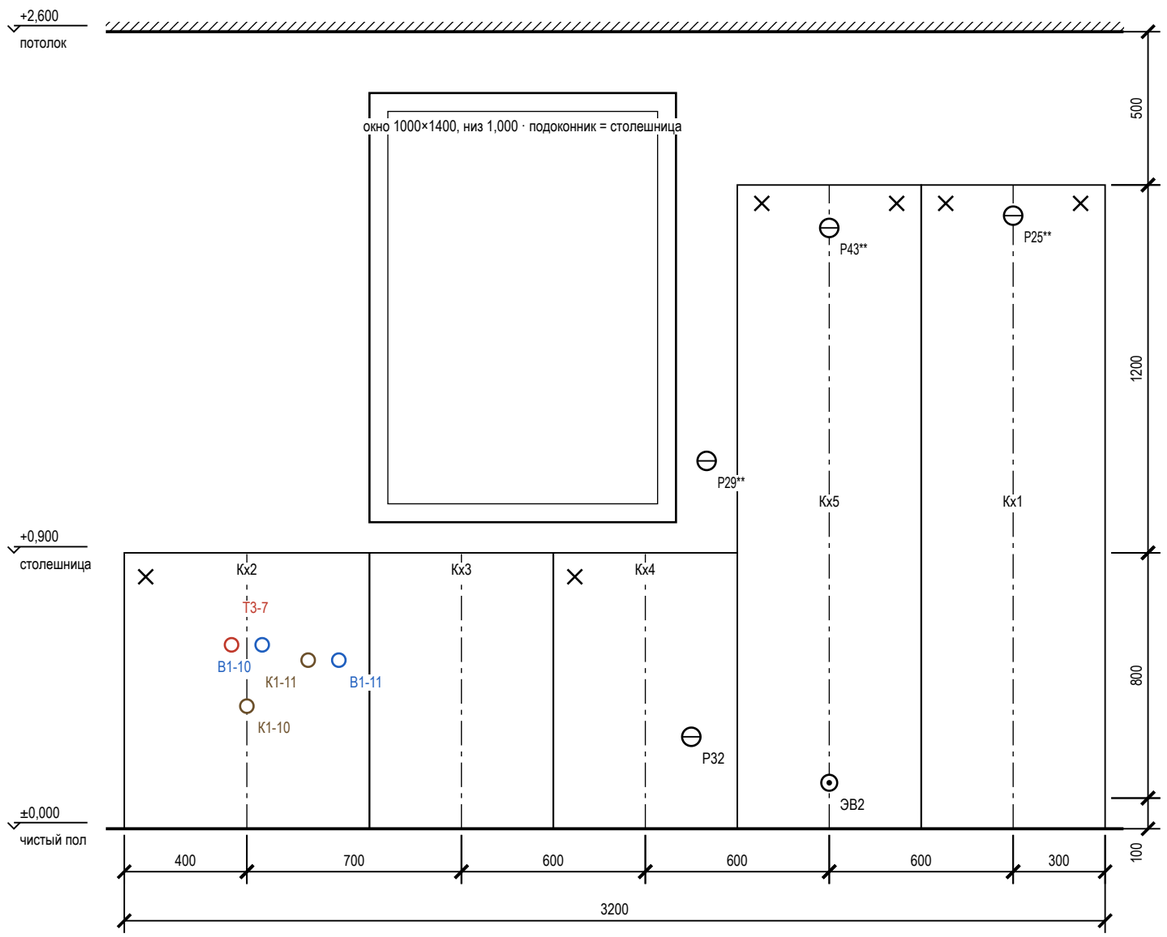

План столешницы

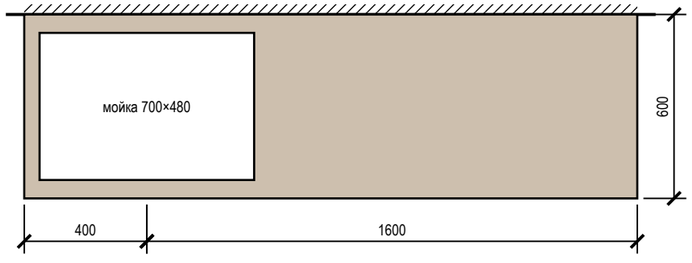

Привязка выводов к осям модулей

Код	Назначение	Модуль	От оси, мм	H, мм	Размещение
Т3-7	Т3 — межос. 100	Кх2	−50	600	в модуле мойки
К1-10	К1 Ø50 — мойка	Кх2	0	400	в модуле мойки
В1-10	В1 — межос. 100	Кх2	+50	600	в модуле мойки
К1-11	К1 Ø40 — слив ПММ в шкафу мойки	Кх2	+200	550	в модуле мойки
В1-11	В1 — кран ПММ в шкафу мойки	Кх2	+300	550	в модуле мойки
Р32	розетка — посудомоечная машина — в соседнем модуле, за ящиком	Кх4	+150	300	в соседнем модуле, за ящиком
Р29**	розетка — фартук	Кх4	+200	1200	над столешницей (фартук)
ЭВ2	вывод кабеля — духовой шкаф — в цоколе	Кх5	0	150	за ящиком под нишей, доступ через ящик
Р43**	розетка — СВЧ — над нишей, съёмная панель	Кх5	0	1960	над нишами техники, за съёмной панелью антресоли
Р25**	розетка — холодильник — над нишей, съёмная панель	Кх1	0	2000	над нишей холодильника, съёмная панель

Зазоры под отделку

Поверхность	Отделка	Зазор, мм	Учесть
фартук	керамогранит	10	от чернового основания до корпуса навесных и столешницы
стены	окраска	5	под штукатурку и шпаклёвку за пеналом
пол	инженерная доска		цоколь — после укладки пола, опоры ±20 мм

Условные обозначения

- нижний модуль, пенал (контур)
- ось модуля (от неё — привязка вывода)
- анкер / уголок крепления к стене
- розетка на стене
- вывод кабеля к технике
- В1 — вывод воды В1 / Т3, канализации К1

Допущения и предложения на листе

Основа листа: размеры сняты с растрового плана заказчика с частичными размерами: рисунок не в масштабе, помещения выровнены по подписанным размерам мебели и проходов; контрольный обмер не выполнен (К-1); высота потолка 2700 мм принята: на плане заказчика её нет (К-2); толщины стен 300 / 120 мм приняты по плану заказчика, не замерены (К-1); разрешённая мощность 15 кВт принята по типовым ТУ для квартиры, ТУ заказчиком не переданы (К-4); подрайон климата не задан — принят не северный (жилые от 2,5 м) (К-6).
Знак «**» — предложение проектировщика, заказчиком не утверждено (согласовать с заказчиком): Р25 — высота 2000 мм выше нормы 1 м (ПУЭ 6.6.30) по назначению: розетка встроенного прибора — в колонне Кх1 над нишей, в антресоли за съёмной панелью; Р29 — Сдвиг под раскладку плитки фартука (стена А) на 100 мм выше — ось на шве или в центре плитки, привязка по таблице листа; Р43 — высота 1960 мм выше нормы 1 м (ПУЭ 6.6.30) по назначению: розетка встроенного прибора — в колонне Кх5 над нишей, в антресоли за съёмной панелью.
См. лист открытых вопросов (лист 6, записи К-1, К-2, К-4, К-6).

Примечания

1. Окно над Кх3, Кх4: низ проёма на 1000 мм от пола, столешница на 900 мм; примыкание столешницы к откосу и подоконнику — до решения: нужно решение заказчика (створка глухая или поворотно-откидная, поднять подоконник); столешницу у окна не раскраивать до решения.
2. Выводы — по проекту электрики и ВК; привязка по горизонтали — от оси модуля (плюс — вправо по виду), по высоте — от чистого пола до оси вывода.
3. Пенал — уголки к стене 2 шт. сверху; нижние модули — стяжками между собой и уголком к стене; ряд выставить по уровню опорами цоколя.
4. Розетки над столешницей — не ниже 150 мм над ней и не за корпусом техники; розетка за ПММ, духовым шкафом и холодильником — только в соседнем модуле или в зоне цоколя с доступом.
5. Столешница — вырезы по шаблонам выбранных моделей мойки и варочной панели; торцы у стены — герметик, пристеночный плинтус.

1000 мм · печать 1:1

Изм.	Кол.уч	Лист	№ док.	Подп.	Дата
Разраб.		Кырлан А.С.			04.11.26
Пров.					
ГИП					
Н. контр.					
Утв.					

ГД-2026-008-АИ

Квартира с кабинетом

Общая площадь 127,29* м² · * размеры со скана, не замерены (реестр — л. 6–8, К-1)

Дизайн-проект интерьера

Стадия	Лист	Листов
РП	79	131

Кухня (пом. 4). Монтажная схема

М 1:20

Кырлан Александр Сергеевич


выпуск 04.11.2026 № 4177cbe7a3 · стр. 87 из 166

Остров Кх6 (пом. 4). Чертёж изделия

ПРЕДВАРИТЕЛЬНО · не для производства работ · открыто пунктов: 13 (реестр — л. 6–8)


Кухня-гостиная (пом. 4) · остров 900×1400 с варочной панелью, столешница — травертин · размеры в мм, отметки от чистого пола

План (вид сверху)

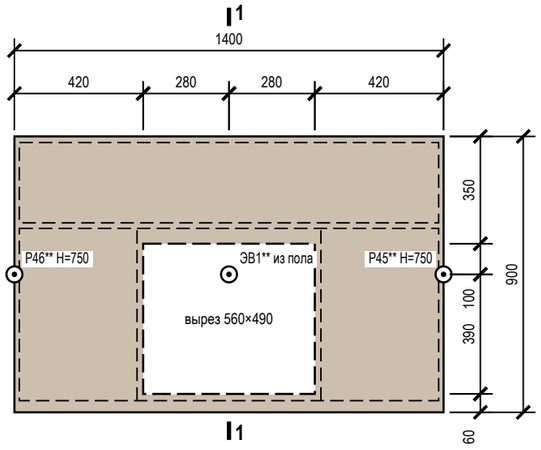


▲ рабочая сторона — западная (к стене Г), проход 1240


Вид с рабочей стороны

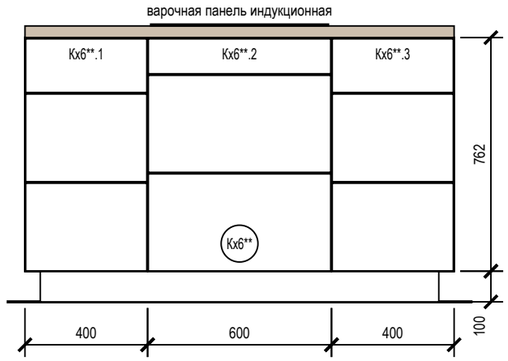

Вид без фасадов (наполнение, вывод)

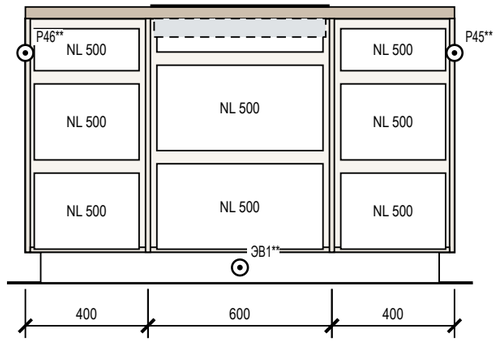

Разрез 1-1 через варочную

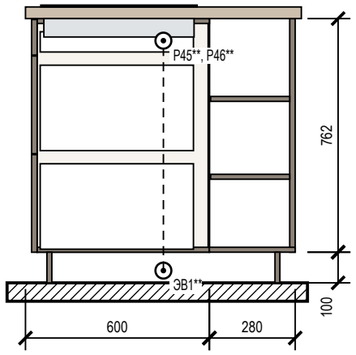

Вид с тыльной стороны

Условные обозначения

- фасад распашной: линии сходятся к стороне петель
- фасад ящика, карго
- столешница
- встраиваемая техника
- деталь в разрезе
- невидимый контур: навесной модуль, корпус под столешницей
- К1 — марка изделия или модуля (на схеме расположения под ней — лист изделия)
- вывод кабеля к технике

Примечания

1. Размеры — в мм по чистовому полу; перед раскроем — контрольный замер цеха после укладки пола. Остров крепится к полу (уголки в цоколе), выравнивается опорами ±20 мм.
2. Корпуса — ЛДСП 16 мм, задняя стенка ХДФ 4 мм; фасады — МДФ, эмаль матовая 18 мм; столешница 38 мм (материал — по наименованию изделия: столешница травертин), свес 20 мм по периметру; цоколь 100 мм с отступом 50 мм.
3. Кромка: скрытые торцы 0,4 мм, видимые 2 мм. Номинальные зазоры: между фасадами 3 мм, фасад — столешница 3 мм.
4. Рабочая сторона — западная (к стене Г): проход 1240 мм; с тыла — открытые полки глубиной 262 мм. Членение и сторона — предложение мебельщика.
5. Варочная панель индукционная 60 см: вырез 560×490, передняя кромка выреза в 60 мм от рабочего края; верхний ящик под панелью — с зазором 40 мм под корпус панели (вентиляция индукции); размеры выреза — по шаблону выбранной модели.
6. Питание: ЭВ1** — варочная панель на острове — вывод из пола под островом, в цоколе; Р45** — столешница острова — в торцевой панели, Н=750; Р46** столешница острова — в торцевой панели, Н=750; кабель — внутри модуля до панели, доступ через съёмный цоколь.
7. Вытяжка над островом — островная потолочная, режим рециркуляции (угольный фильтр), ширина 900, низ +1550; низ — не ниже 650 мм над панелью или по паспорту модели.

Спецификация изделия Кх6**

Поз.	Наименование	Тип, размер	Кол.
Кх6**.1	модуль с ящиками	400×900×900	1
Кх6**.2	модуль под варочную панель	600×900×900	1
Кх6**.3	модуль с ящиками	400×900×900	1
Кх6**.2	Варочная панель индукционная, 60 см	вырез 560 × 490, кромка выреза в 60 от рабочего края	1
	Направляющие полного выдвижения с доводчиком NL 500	пара	9
	Ручка-профиль	латунь матовая	9
	Опора кухонная регулируемая 100–120 мм	+ клипса цоколя	12
	Уголок крепления острова к полу	стальной, в цоколе	4
	Полкодержатель с фиксацией	ø5 мм	24

Допущения и предложения на листе

Основа листа: размеры сняты с растрового плана заказчика с частичными размерами: рисунок не в масштабе, помещения выровнены по подписанным размерам мебели и проходов; контрольный обмер не выполнен (К-1); высота потолка 2700 мм принята: на плане заказчика её нет (К-2); толщины стен 300 / 120 мм приняты по плану заказчика, не замерены (К-1); разрешённая мощность 15 кВт принята по типовым ТУ для квартиры, ТУ заказчиком не переданы (К-4); подрайон климата не задан — принят не северный (жилые от 2,5 м) (К-6).
Знак «**» — предложение проектировщика, заказчиком не утверждено (согласовать с заказчиком): ЭВ1 — вывод из пола под островом Кх6: трасса в конструкции пола (стяжка, толщина — по обмеру) и лючок в цоколе — согласовать с заказчиком и изготовителем кухни; Р45, Р46 — на фартуке у стены место только под 1 пост(а) (окно над столешницей, мойка, колонны), практика — не меньше 4 над рабочей поверхностью: розетки в торцевой панели острова Кх6, питание из пола под островом той же трассой, что вывод варочной — согласовать с заказчиком и изготовителем кухни; ИЗ-8: Кх6 — Остров сдвинут от кухонного ряда: торец острова стоял в 900 мм от фронта ПММ Кх3 и модуля Кх4 — меньше 1000 мм (СП 31-107-2004, п. 6.1.12) и меньше 1200 мм, при которых открытые ПММ и ящики не перекрывают проход.
См. лист открытых вопросов (лист 6, записи К-1, К-2, К-4, К-6; лист 8, запись ИЗ-8).

1000 мм · печать 1:1

Изм.	Кол.уч	Лист	№ док.	Подп.	Дата
Разраб.		Кырлан А.С.			04.11.26
Пров.					
ГИП					
Н. контр.					
Утв.					

ГД-2026-008-АИ

Квартира с кабинетом

Общая площадь 127,29* м² · * размеры со скана, не замерены (реестр — л. 6–8, К-1)

Дизайн-проект интерьера

Стадия	Лист	Листов
РП	80	131

Остров Кх6 (пом. 4). Чертёж изделия

М 1:20

Кырлан Александр Сергеевич


выпуск 04.11.2026 · 4177cbe7a3 · стр. 88 из 166

Шкафы. Монтажная схема. Лист 1 из 2


ПРЕДВАРИТЕЛЬНО · не для производства работ · открыто пунктов: 13 (реестр — л. 6–8)

крепление к стене, установочные размеры, зазоры под отделку · размеры в мм


Система хранения Г1 (пом. 2)

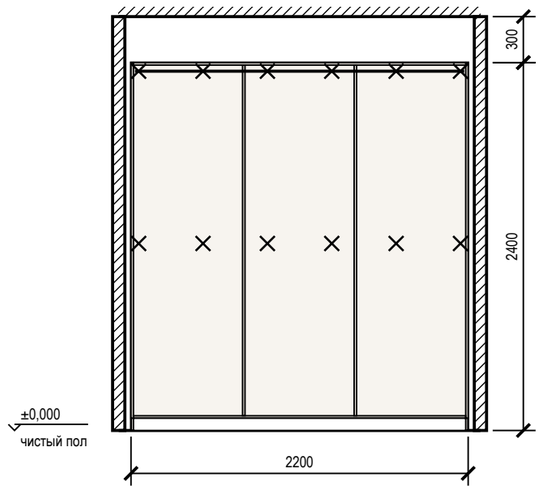


Система хранения Г2 (пом. 2)

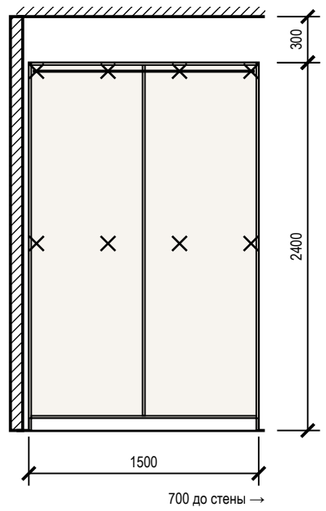

Шкаф распашной Кб1 (пом. 3)

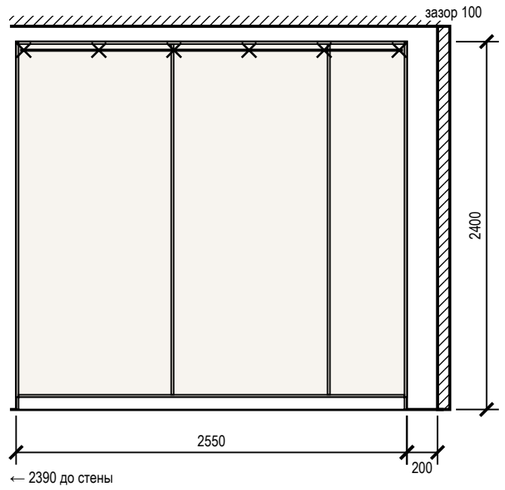

ТВ-стена Кх12* (пом. 4)

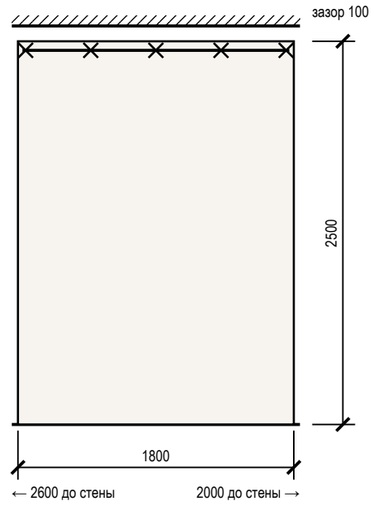

Крепление и зазоры под отделку (изделия листа 1)

Марка	Помещение, стена	Основание	Отделка стены	Зазор, мм	Крепёж по планке	От опрокидывания
Г1	Гардеробная-постирочная (2), стена Г	по основанию — см. таблицу крепежа	окраска	5	анкер 12 шт. (2 ряда)	крепление к стене, 3 точки
Г2	Гардеробная-постирочная (2), стена В	по основанию — см. таблицу крепежа	окраска	5	анкер 8 шт. (2 ряда)	крепление к стене, 3 точки
Кб1	Кабинет (3), стена Г	по основанию — см. таблицу крепежа	окраска	5	анкер 6 шт., шаг 490	уголки 2 шт.
Кх12*	Кухня-гостиная (4), стена Б	по основанию — см. таблицу крепежа	окраска	5	анкер 5 шт., шаг 425	уголки 2 шт.

Крепёж по основанию стены

Основание стены	Крепёж
бетон, ж/б	анкер-шуруп 7,5×72 или дюбель 8×60 с шурупом 5×70
кирпич полнотелый	дюбель 8×80 с шурупом 5×90
газобетон, пазогребень	дюбель для газобетона 10×100 или химический анкер
гипсокартон	закладная до обшивки (брус 40×80 или фанера 18 мм), саморез в закладную

Условные обозначения

- анкер / уголок крепления к стене
- корпус и полки ЛДСП (вид на стену)
- компенсатор — короб до потолка

Примечания

1. Установочные размеры — от чистого пола и чистых стен; перед установкой контрольный замер после отделки.
2. Порядок: корпус выставить по уровню опорами цоколя → закрепить к стене по задней планке → навесить двери и фасады, отрегулировать зазоры → подогнать и закрепить компенсатор.
3. Анкеры — с шагом не более 500 мм, не ближе 50 мм от края планки; на ГКЛ только в закладную, установленную до обшивки.
4. Скрытые коммуникации под анкеры проверить детектором; трассы электрики по плану розеток.
5. Сборка стоя на месте: Кх12* — корпус не собирается лёжа и не поднимается собранным, а собирается в проектном положении у стены; выставление по уровню и крепление к стене выполняются по корпусу, собранному на месте.
6. Монтажная схема на 2 листах, лист 1 из 2; продолжение — на следующем листе схемы. Условные обозначения, таблица крепежа по основанию и примечания повторены на каждом листе.

Допущения и предложения на листе

Основа листа: размеры сняты с растрового плана заказчика с частичными размерами: рисунок не в масштабе, помещения выровнены по подписанным размерам мебели и проходов; контрольный обмер не выполнен (К-1); высота потолка 2700 мм принята: на плане заказчика её нет (К-2); толщины стен 300 / 120 мм приняты по плану заказчика, не замерены (К-1); разрешённая мощность 15 кВт принята по типовым ТУ для квартиры, ТУ заказчиком не переданы (К-4); подрайон климата не задан — принят не северный (жилые от 2,5 м) (К-6). Знак «*» — принято, не замерено и не подтверждено (замерить на объекте): ИЗ-5, ИЗ-9, К-20: Кх12 — Было: предмет 1800×400 h 500 на отметке 0 — на развёртке стены Б низкий короб у пола.

См. лист открытых вопросов (лист 6, записи К-1, К-2, К-4, К-6; лист 7, запись К-20; лист 8, записи ИЗ-5, ИЗ-9).

1000 мм · печать 1:1

Изм.	Кол.уч	Лист	№ док.	Подп.	Дата
Разраб.		Кырлан А.С.			04.11.26
Пров.					
ГИП					
Н. контр.					
Утв.					

ГД-2026-008-АИ

Квартира с кабинетом

Общая площадь 127,29* м² · * размеры со скана, не замерены (реестр — л. 6–8, К-1)

Дизайн-проект интерьера

Стадия	Лист	Листов
РП	81	131

Шкафы. Монтажная схема. Лист 1 из 2

М 1:40

Кырлан Александр Сергеевич


выпуск 04.11.2026 № 4177cbe7a3 · стр. 89 из 166

Шкафы. Монтажная схема. Лист 2 из 2


ПРЕДВАРИТЕЛЬНО · не для производства работ · открыто пунктов: 13 (реестр — л. 6–8)

крепление к стене, установочные размеры, зазоры под отделку · размеры в мм


Шкаф распашной Кх13 (пом. 4)

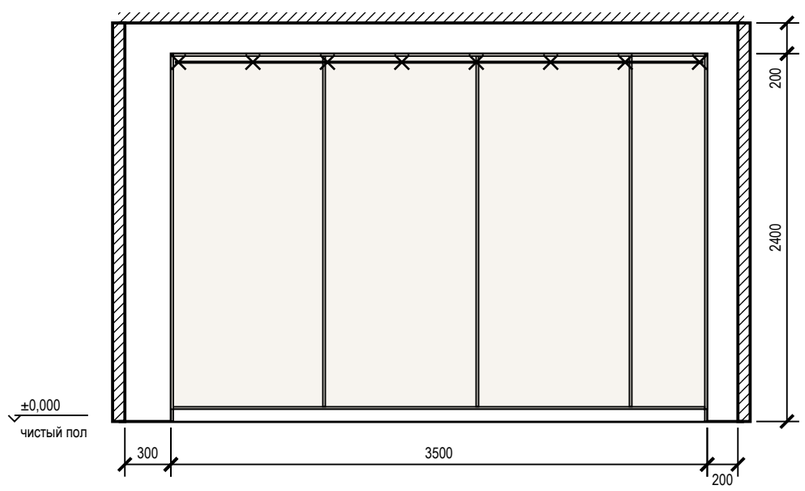


Шкаф распашной Дт1 (пом. 6)

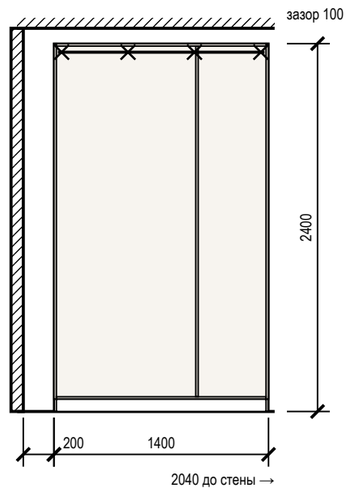

Тумба под раковину Вн1 (пом. 7)**

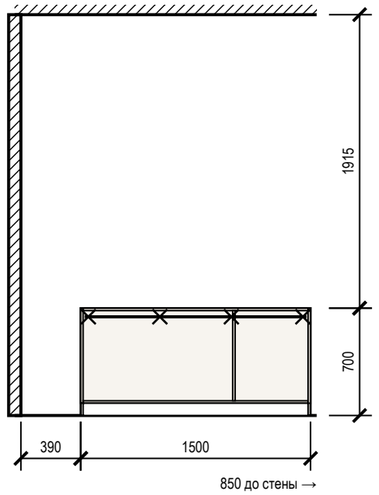

Шкаф-купе Пх1 (пом. 8)**

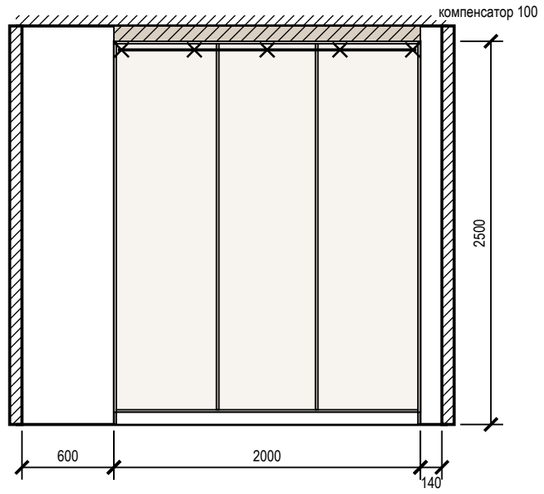

Крепление и зазоры под отделку (изделия листа 2)

Марка	Помещение, стена	Основание	Отделка стены	Зазор, мм	Крепёж по планке	От опрокидывания
Кх13	Кухня-гостиная (4), стена В	по основанию — см. таблицу крепежа	окраска	5	анкер 8 шт., шаг 486	уголки 2 шт.
Дт1	Детская (6), стена А	по основанию — см. таблицу крепежа	окраска	5	анкер 4 шт., шаг 433	крепление к стене, 2 точки
Вн1**	Ванная (7), стена Б	по основанию — см. таблицу крепежа	плитка	10	анкер 4 шт., шаг 467	крепление к стене, 2 точки
Пх1**	Прихожая (8), стена Г	по основанию — см. таблицу крепежа	окраска	5	анкер 5 шт., шаг 475	уголки 2 шт.

Крепёж по основанию стены

Основание стены	Крепёж
бетон, ж/б	анкер-шуруп 7,5×72 или дюбель 8×60 с шурупом 5×70
кирпич полнотелый	дюбель 8×80 с шурупом 5×90
газобетон, пазогребень	дюбель для газобетона 10×100 или химический анкер
гипсокартон	закладная до обшивки (брус 40×80 или фанера 18 мм), саморез в закладную

Условные обозначения

- анкер / уголок крепления к стене
- корпус и полки ЛДСП (вид на стену)
- компенсатор — короб до потолка

Примечания

1. Установочные размеры — от чистого пола и чистых стен; перед установкой контрольный замер после отделки.
2. Порядок: корпус выставить по уровню опорами цоколя → закрепить к стене по задней планке → навесить двери и фасады, отрегулировать зазоры → подогнать и закрепить компенсатор.
3. Анкеры — с шагом не более 500 мм, не ближе 50 мм от края планки; на ГКЛ только в закладную, установленную до обшивки.
4. Скрытые коммуникации под анкеры проверить детектором; трассы электрики по плану розеток.
5. Монтажная схема на 2 листах, лист 2 из 2. Условные обозначения, таблица крепежа по основанию и примечания повторены на каждом листе.

Допущения и предложения на листе

Основа листа: размеры сняты с растрового плана заказчика с частичными размерами: рисунок не в масштабе, помещения выровнены по подписанным размерам мебели и проходов; контрольный обмер не выполнен (К-1); высота потолка 2700 мм принята: на плане заказчика её нет (К-2); толщины стен 300 / 120 мм приняты по плану заказчика, не замерены (К-1); разрешённая мощность 15 кВт принята по типовым ТУ для квартиры, ТУ заказчиком не переданы (К-4); подрайон климата не задан — принят не северный (жилые от 2,5 м) (К-6). Знак «**» — предложение проектировщика, заказчиком не утверждено (согласовать с заказчиком): ИЗ-1: Пх1 — фасад купе по кадру визуализации прихожей: МДФ 10 мм, эмаль матовая, латунный профиль, зеркальные арочные вставки (поле 100 мм); ИЗ-2: Вн1 — Тумба 1500 под раковины П2 и П3 — по описанию модели автора («две на тумбе 1500»): ширина из модели, глубина 500 под раковины 450 и высота столешницы 700 под борт раковин 850, тумба напольная — низ на чистом полу (elevation 0) — предложение проектировщика; выводы ВК под раковинами закрывает тумба.
См. лист открытых вопросов (лист 6, записи К-1, К-2, К-4, К-6; лист 7, записи ИЗ-1, ИЗ-2).

1000 мм · печать 1:1

Изм.	Кол.уч	Лист	№ док.	Подп.	Дата
Разраб.		Кырлан А.С.			04.11.26
Пров.					
ГИП					
Н. контр.					
Утв.					

ГД-2026-008-АИ

Квартира с кабинетом

Общая площадь 127,29* м² · * размеры со скана, не замерены (реестр — л. 6–8, К-1)

Дизайн-проект интерьера

Стадия	Лист	Листов
РП	82	131

Шкафы. Монтажная схема. Лист 2 из 2

М 1:40

Кырлан Александр Сергеевич

выпуск 04.11.2026 № 4177cbe7a3 · стр. 90 из 166

Ведомости изделий, техники и фурнитуры

встроенная мебель и кухонный гарнитур · размеры в мм

Ведомость изделий

Марка	Наименование	Пом.	Ш×Г×В, мм	Корпус	Фасад	Кромка, мм	Кол.
Г1	Система хранения	2	2200×600×2400	ЛДСП 16	без фасадов	0,4 / 2	1
Г2	Система хранения	2	1500×550×2400	ЛДСП 16	без фасадов	0,4 / 2	1
Кб1	Шкаф распашной	3	2550×600×2400	ЛДСП 16	МДФ 18 мм, эмаль матовая; арочная фрезеровка филёнки (полукруглый верх, поле 100 мм)	0,4 / 2	1
Кх12*	ТВ-стена	4	1800×400×2500	оцинкованный профиль ПП 60×27 / ПН 28×27 (НГ), на стене Б	панели МДФ 19 мм с волнистым рельефом, эмаль матовая	0,4 / 2	1
Кх13	Шкаф распашной	4	3500×500×2400	ЛДСП 16	МДФ 18 мм, эмаль матовая	0,4 / 2	1
Дт1	Шкаф распашной	6	1400×600×2400	ЛДСП 16	МДФ 18 мм, эмаль матовая	0,4 / 2	1
Вн1**	Тумба под раковину	7	1500×500×700	ЛДСП 16	МДФ 18 мм, эмаль матовая	0,4 / 2	1
Пх1**	Шкаф-купе	8	2000×600×2500	ЛДСП 16	МДФ 10 мм, эмаль матовая в профиле: алюминий, латунь матовая; вставка — зеркало серебро 4 мм, плёнка безопасности, арочная (полукруглый верх, поле 100 мм)	0,4 / 2	1
Кх2	Модуль нижний: мойка	4	800×600×900	ЛДСП 16	МДФ 18 мм, эмаль матовая	0,4 / 2	1
Кх3	Модуль под ПММ 60: без корпуса, фасад на дверь машины	4	600×600×900	без корпуса	МДФ 18 мм, эмаль матовая — на дверь машины (навеска из её комплекта), цоколь		1
Кх4	Модуль нижний: ящики	4	600×600×900	ЛДСП 16	МДФ 18 мм, эмаль матовая	0,4 / 2	1
Кх5	Пенал: духовой шкаф, СВЧ	4	600×600×2100	ЛДСП 16	МДФ 18 мм, эмаль матовая	0,4 / 2	1
Кх1	Пенал: холодильник встр.	4	600×650×2100	ЛДСП 16	МДФ 18 мм, эмаль матовая	0,4 / 2	1
Кх6**	Остров (Кх6**.1, Кх6**.2, Кх6**.3)	4	1400×900×900	ЛДСП 16	МДФ 18 мм, эмаль матовая	0,4 / 2	1
Кх7	банкетка-диван вдоль окон, бархат — экран радиатора, изготовление на заказ РО-6*: решётка в лицевой панели, щель 60, зазор 50	4	3200×600×850	по чертежу	решётка по ширине прибора	0,4 / 2	1

Ведомость встраиваемой техники

Поз.	Прибор	Ниша, вырез, мм	Вентиляция	Питание	Схема
Кх2	Мойка врезная / подстольная с сифоном	вырез по шаблону, ориентир 700 × 480		смеситель — выводы ВК	по модели
Кх3	Посудомоечная машина встраиваемая, 60 см	ниша 600 × 862 (от пола до низа столешницы)	зазор в цоколе, по схеме	Р32: Кх4, Н=300 — в соседнем модуле, за ящиком	по модели
Кх5	Духовой шкаф встраиваемый, 60 см	ниша 568 × 600, глубина ≥ 550; низ +820	зазор 50 за прибором, без задней стенки; щель 50 в полке	ЭВ2: Кх5, Н=150 — за ящиком под нишей, доступ через ящик	по модели
Кх5	СВЧ-печь встраиваемая, 38 см	ниша 568 × 380, глубина ≥ 550; низ +1436	зазор 50 за прибором, без задней стенки; щель 50 в полке	Р43**: Кх5, Н=1960 — над нишами техники, за съёмной панелью антресоли	по модели
Кх1	Холодильник встраиваемый, ниша 1780	ниша 1780 × 560 × 550	решётка в цоколе, канал за корпусом, выход сверху	Р25**: Кх1, Н=2000 — над нишей холодильника, съёмная панель	по модели
Кх6**.2	Варочная панель индукционная, 60 см	вырез в столешнице 560 × 490, кромка выреза в 60 от рабочего края	зазор 40 мм под корпусом панели над верхним ящиком	ЭВ1**: вывод из пола под островом, в цоколе, 700 мм от левого торца, 450 мм от рабочего края	по модели

Примечания

1. Модели техники выбирает заказчик до изготовления мебели; ниши, вырезы и вентиляция — по монтажной схеме выбранной модели (условие гарантии), её номер вносится в ведомость.
2. Количество фурнитуры — по чертежам изделий; запас крепежа 5 %. Аналоги — по характеристикам (доводчик, нагрузка, ход).
3. Цвет корпусов, фасадов и профилей — по колерной карте проекта. Кромка — скрытые / видимые торцы, мм.

Ведомость фурнитуры

№	Фурнитура	Тип, размер	Изделия	Кол.
1	Полкодержатель с фиксацией	ø5 мм	Г1, Г2, Кб1, Кх13, Дт1, Вн1**, Пх1**, Кх5, Кх1, Кх6**	236
2	Штанга овальная 30×15, L = 712	+ 2 держателя	Г1	3
3	Опора регулируемая с цоколем на клипсах	ход 20 мм	Г1, Г2, Кб1, Кх13, Дт1, Вн1**, Пх1**	56
4	Анкер по основанию стены	по таблице крепежа	Г1, Г2, Кб1, Кх12*, Кх13, Дт1, Вн1**, Пх1**	52
5	Уголок крепления к стене от опрокидывания	стальной	Г1, Г2, Кб1, Кх12*, Кх13, Дт1, Вн1**, Пх1**, Кх5, Кх1	20
6	Штанга овальная 30×15, L = 726	+ 2 держателя	Г2	1
7	Петля накладная 110° с доводчиком	чашка 35 мм	Кб1, Кх13, Дт1, Вн1**, Кх2, Кх5, Кх1	109
8	Штанга овальная 30×15, L = 996	+ 2 держателя	Кб1	2
9	Штанга овальная 30×15, L = 486	+ 2 держателя	Кб1	1
10	Штанга выдвижная торцевая	L по глубине	Кх13	2
11	Штанга овальная 30×15, L = 909	+ 2 держателя	Дт1	1
12	Система дверей купе: профиль, направляющие, ролики	на 3 двери	Пх1**	1
13	Ручка-профиль вертикальная	в цвет профиля	Пх1**	3
14	Штанга овальная 30×15, L = 653	+ 2 держателя	Пх1**	3
15	Полка для обуви выдвижная наклонная	ширина 630	Пх1**	2
16	Полка для обуви выдвижная наклонная	ширина 653	Пх1**	1
17	Ручка-профиль	латунь матовая	Кх2, Кх3, Кх4, Кх5, Кх1, Кх6**	21
18	Опора кухонная регулируемая 100–120 мм	+ клипса цоколя	Кх2, Кх4, Кх5, Кх1, Кх6**	30
19	Комплект навески фасада ПММ	из поставки машины	Кх3	1
20	Направляющие полного выдвижения с доводчиком NL 500	пара	Кх4, Кх5, Кх6**	14
21	Уголок крепления острова к полу	стальной, в цоколе	Кх6**	4

Допущения и предложения на листе. Основа листа: размеры сняты с растрового плана заказчика с частичными размерами: рисунок не в масштабе, помещения выровнены по подписанным размерам мебели и проходов; контрольный обмер не выполнен (К-1); высота потолка 2700 мм принята: на плане заказчика её нет (К-2); толщины стен 300 / 120 мм приняты по плану заказчика, не замерены (К-1); разрешённая мощность 15 кВт принята по типовым ТУ для квартиры, ТУ заказчиком не переданы (К-4); подрайон климата не задан — принят не северный (жилые от 2,5 м) (К-6). Знак «*» — принято, не замерено (замерить): ИЗ-5, ИЗ-9, К-20: Кх12; ИЗ-7, К-1, К-19: РО-6. Знак «**» — предложено, не утверждено (согласовать): Р25, ЭВ1, Р43; ИЗ-1: Пх1; ИЗ-2: Вн1; ИЗ-8: Кх6. См. лист открытых вопросов (лист 6, записи К-1, К-2, К-4, К-6; лист 7, записи ИЗ-1, ИЗ-2, К-19, К-20; лист 8, записи ИЗ-5, ИЗ-7–ИЗ-9).

Изм.	Кол.уч	Лист	№ док.	Подп.	Дата

Разраб.	Кырлан А.С.		04.11.26
Пров.			
ГИП			
Н. контр.			
Утв.			

ГД-2026-008-АИ

Квартира с кабинетом

Общая площадь 127,29* м² · * размеры со скана, не замерены (реестр — л. 6–8, К-1)

Дизайн-проект интерьера	Стадия	Лист	Листов
	РП	83	131
Ведомости изделий, техники и фурнитуры М б/м	**Кырлан Александр Сергеевич**		

выпуск 04.11.2026 № 4177cbe7a3 · стр. 91 из 166

09

Развёртки и узлы

Кырлан Александр Сергеевич

выпуск 04.11.2026 № 4177cbe7a3 · стр. 92 из 166

Реестр марок отделки и позиций альбома

Реестр марок отделки (О ↔ позиции колерной карты) и марки позиций по видам

Реестр марок отделки альбома

Марка	Поверхность	Материал, изделие	Цвет, код	Помещения	Колер. карта
О1	стены	окраска, Farrow & Ball Modern Emulsion, матовая, подготовка Q3	Farrow & Ball No. 15 «Bone — мягкий каменно-серый с зеленцой»	1, 3, 4, 5, 6, 8	К1
О2	акцентная стена	окраска, Farrow & Ball Modern Emulsion, матовая, подготовка Q3	Farrow & Ball No. 34 «Calke Green традиционный шалфей»	1, 3, 4, 6	К2
О3	плинтус	плинтус МДФ, h 80 мм, аналог: плинтус МДФ под покраску 80×16	Farrow & Ball No. 15 «Bone — мягкий каменно-серый с зеленцой»	1, 3, 4, 5, 8	К4
О4	потолок	окраска, Tikkurila Anti-Reflex 2, глубокоматовая, подготовка Q3	Tikkurila V503 «Winter»	1, 2, 3, 4, 5, 6, 8	К3
О5	пол	инженерная доска, Coswick Вековые традиции, 2100×127 мм, 1167-4250		1, 2, 3, 4, 5, 6	КМ1
О6	стены	окраска, Tikkurila Harmony, матовая, подготовка Q3	Tikkurila V503 «Winter»	2	К5
О7	плинтус	плинтус МДФ, h 80 мм, аналог: плинтус МДФ под покраску 80×16	Tikkurila V503 «Winter»	2	К6
О8	фартук	керамогранит, 1200×600×9 мм, аналог: керамогранит под травертин, матовый, затирка CG2WA		4	КМ2
О9	плинтус	плинтус МДФ, Orac Decor Contour (Luxxus), h 69 мм, SX165	Farrow & Ball No. 15 «Bone — мягкий каменно-серый с зеленцой»	6	К7
О10	стены	облицовка плиткой, Atlas Concorde Marvel Travertine, 600×1200×9 мм, A8UZ, затирка CG2WA	Atlas Concorde A8UZ «Marvel Travertine»	7, 9	КМ3
О11	потолок	окраска, Tikkurila Luja 7, матовая, подготовка Q3	Tikkurila V503 «Winter»	7, 9	К8
О12	пол	керамогранит, 600×600×9 мм, аналог: керамогранит ректифицированный под травертин, матовый, затирка CG2WA		7, 9	КМ4
О13	пол	керамогранит, Atlas Concorde Marvel Travertine, 600×1200×9 мм, A8UZ, затирка CG2WA	Atlas Concorde A8UZ «Marvel Travertine»	8	КМ5

Марки позиций альбома по видам

Префикс	Что обозначает, позиции	Листы
Д	двери: Д-1–Д-7	15–18
ПР	проёмы без полотна (порталы): ПР-1, ПР-2	15–18
ОК	окна: ОК-1–ОК-6	15–18
Вн, Г, Дт, Кб, Кх, Пх, С	мебель и оборудование: Вн1**, Г1, Г2, Дт1, Дт2**, Дт4, Кб1–Кб4, Кб5**, Кб6, Кб7, Кх1–Кх5, Кх6**, Кх7, Кх8**, Кх9**, Кх10, Кх12*, Кх13, Пх1**, Пх2, С1–С5, С6**	19–24
П	сантехнические приборы: П1**, П2–П7, П10**, П11, П12, П13**	36–46
ДК	декор (картины, зеркала, растения): ДК1, ДК2**, ДК3–ДК9, ДК10**, ДК11**	1, 63–68
Т	текстиль (шторы, ковры): Т1**, Т2**, Т3–Т21, Т22**, Т23–Т26, Т27**, Т28**	1, 63–68

Допущения и предложения на листе. Знак «*» принято (замерить). Знак «**» предложено (согласовать): плинтус пом. 1–5, 8, фартук пом. 4, пол пом. 7, 9. См. лист открытых вопросов (листы 6–8).

Марки позиций альбома по видам (продолжение)

Префикс	Что обозначает, позиции	Листы
S	выключатели: S1–S8, S9**, S10**, S11–S16, S17**, S18**	25–33
Р	розетки: Р1, Р2, Р5, Р6, Р7**, Р8**, Р11, Р12**, Р13–Р16, Р17**, Р18**, Р21–Р24, Р25**, Р29**, Р32, Р33**, Р34, Р37, Р39, Р40, Р41**, Р42**, Р43**, Р44, Р45**, Р46**, Р49, Р50	25–33
Св	светильники: Св1–Св14, Св15**, Св16–Св29, Св30**, Св31**, Св32**, Св33**, Св34**, Св35**, Св36**, Св37**, Св38**, Св39**, Св40**, Св41, Св42**, Св43**, Св44**, Св45**, Св46**, Св47**, Св48**, Св49**, Св50, Св51, Св52**, Св53–Св63, Св64**	25–33
БП	блоки питания LED: БП1–БП4, БП6	25–33
ИП	извещатели: ИП1–ИП7	25–33
ТВ	розетки ТВ: ТВ1, ТВ2, ТВ4	25–33
LAN	розетки компьютерные: LAN2–LAN5, LAN6**	25–33
ЭВ	выводы кабеля: ЭВ1**, ЭВ2, ЭВ3**, ЭВ4**, ЭВ5**, ЭВ6**, ЭВ7**	25–33
АР	точки доступа Wi-Fi: АР1**, АР2**	25–33
КУП	электроустановочные изделия: КУП1**, КУП2**	25–33
ЩК, ЩС**	щиты: ЩК, ЩС**	25–33
ДФ	домофон: ДФ1	25–33
Ст В1, Ст К1, Ст К1-3 (кухня), Ст Т3	стояки (системы В1, Т3, К1): Ст В1-1, Ст В1-2, Ст В1-3, Ст К1-1, Ст К1-2, Ст К1-3 (кухня), Ст Т3-1, Ст Т3-2, Ст Т3-3	36–46
О	марки отделки (реестр альбома): О1–О13	2–5, 84–124
К, КМ	позиции колерной карты: К1–К8, КМ1–КМ5	61, 62
РО	радиаторы отопления: РО-1**, РО-2**, РО-3**, РО-4**, РО-5*, РО-6*, РО-7**, РО-8**, РО-9**	34, 35

Примечания

1. Марка отделки О — одна на весь альбом: одна и та же отделка (материал, изделие, цвет, формат) на всех листах имеет одну марку; на развёртках и планах стоят марки этого реестра.
2. Столбец «Колер. карта» — позиции колерной карты (лист 61): К — окраска по коду цвета, КМ — материал без кода цвета; «Помещения» — номера по экспликации; количества — по ведомости отделки помещений (лист 59).
3. Марки позиций: один префикс — один вид позиций на весь альбом (двери Д, окна ОК, мебель М, сантехприборы П, декор ДК, текстиль Т, колерная карта К и КМ, радиаторы РО, розетки Р, выключатели S, светильники Св; стояки — «Ст» и система, например «Ст К1-1»). Совпадение префиксов у разных видов — замечание к исходным данным, при выпуске исправляется в модели.

Изм.	Кол.уч	Лист	№ док.	Подп.	Дата
Разраб.		Кырлан А.С.			04.11.26
Пров.					
ГИП					
Н. контр.					
Утв.					

ГД-2026-008-АИ

Квартира с кабинетом

Общая площадь 127,29* м² · * размеры со скана, не замерены (реестр — л. 6–8, К-1)

Дизайн-проект интерьера

Стадия	Лист	Листов
РП	84	131

Реестр марок отделки и позиций альбома


М б/м

Кырлан Александр Сергеевич

Схема расположения развёрток и узлов

План квартиры: марки развёрток по помещениям, выноски узлов, ведомость «марка → лист»

ПРЕДВАРИТЕЛЬНО · не для производства работ · открыто пунктов: 13 (реестр — л. 6–8)

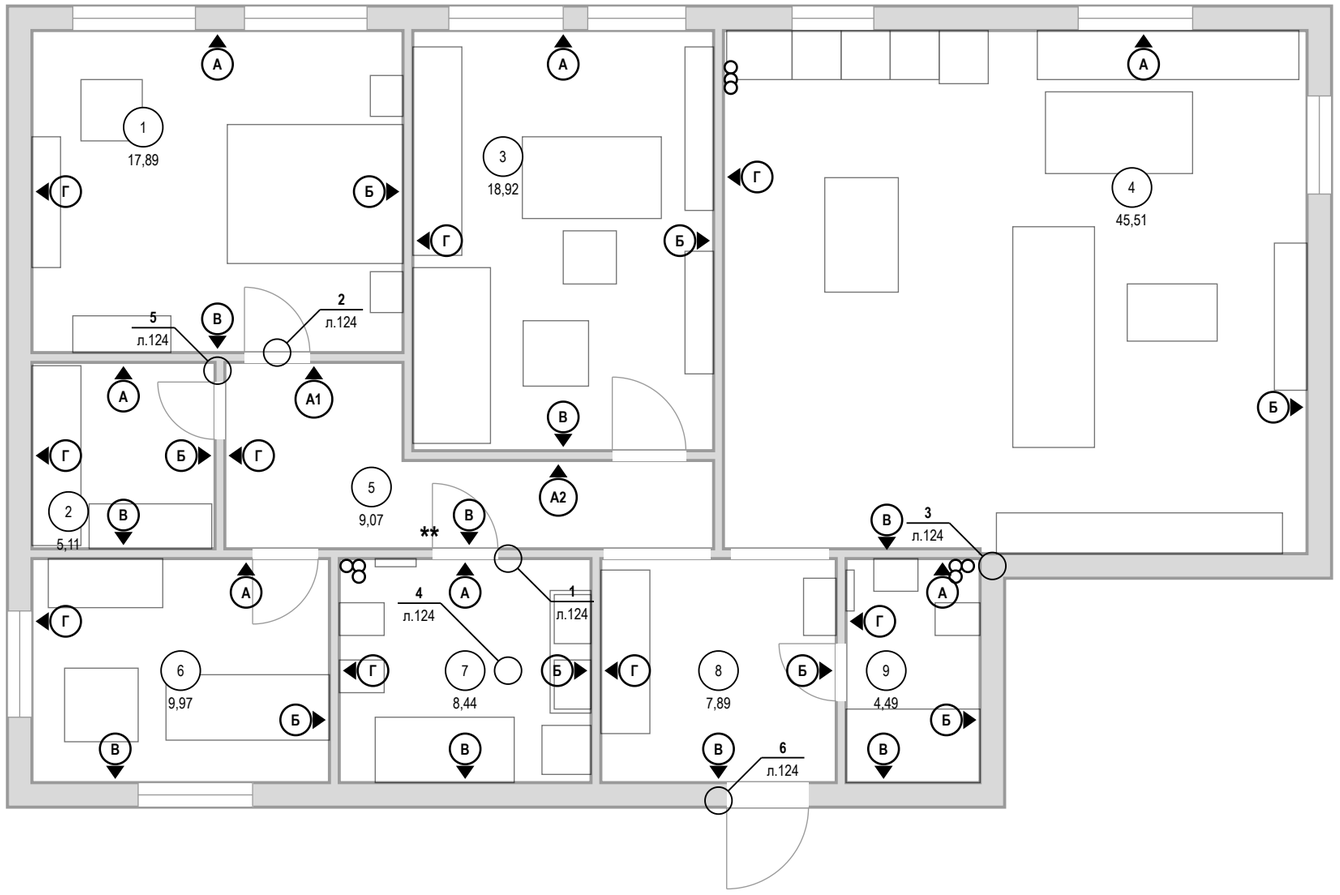

Развёртки и узлы: марка → лист

Марка	Помещение / узел	Лист
А, Б, В, Г	Спальня (пом. 1)	86–90
А, Б, В, Г	Гардеробная-постирочная (пом. 2)	91, 92
А, Б, В, Г	Кабинет (пом. 3)	93–96
Г, А, Б, В	Кухня-гостиная (пом. 4)	97, 98, 100, 101, 103, 104, 106
А1, А2, В, Г	Коридор (пом. 5)	108–110
А, Б, В, Г	Детская (пом. 6)	111–114
А, Б, В, Г	Ванная (пом. 7)	115–118
Б, В, Г	Прихожая (пом. 8)	119, 120
А, Б, В, Г	Санузел гостевой (пом. 9)	121–123
узел 1	Порог 15 мм: мокрая зона — смежное помещение	124
узел 2	Дверь скрытого монтажа в плоскости стены, плинтус	124
узел 3	Короб стояков К1-1 с люком и звукоизоляцией	124
узел 4	Гидроизоляция санузла: заход на стены 200 мм	124
узел 5	Плинтус МДФ 80×16 мм у окрашенной стены по доске (ламинату)	124
узел 6	Плинтус МДФ 80×16 мм у окрашенной стены по керамограниту (плитке)	124

Допущения и предложения на листе

Основа листа: размеры сняты с растрового плана заказчика с частичными размерами: рисунок не в масштабе, помещения выровнены по подписанным размерам мебели и проходов; контрольный обмер не выполнен (К-1); высота потолка 2700 мм принята: на плане заказчика её нет (К-2); толщины стен 300 / 120 мм приняты по плану заказчика, не замерены (К-1); разрешённая мощность 15 кВт принята по типовым ТУ для квартиры, ТУ заказчиком не переданы (К-4); подрайон климата не задан — принят не северный (жилые от 2,5 м) (К-6).

Знак «**» — предложение проектировщика, заказчиком не утверждено (согласовать с заказчиком): ИЗ-2, К-5: дверь пом. 7 (стена А) — Проём сдвинут вдоль стены А от угла Б: offset 2300 → 1200 — утверждено автором (ИЗ-2, Кырлан А.С.).

См. лист открытых вопросов (лист 6, записи К-1, К-2, К-4–К-6; лист 7, запись ИЗ-2).

Условные обозначения

- (А) ▼ — марка развёртки: буква стены, стрелка — взгляд
- ○ — выноска узла: над полкой — узел, под полкой — лист
- (1) — номер помещения, площадь м²

1000 мм · печать 1:1

Примечания

1. Развёртки — вид на стену изнутри помещения; буквы стен — одна система на весь альбом (как на листах выводов, плитки и отделки).
2. Стены без электроточек, мебели, декора и акцентной отделки развёрток не имеют: их отделка — по ведомости отделки помещений.
3. Узлы — на листе узлов; места применения — по выноскам этого листа и ведомости «марка → лист».

Изм.	Кол.уч	Лист	№ док.	Подп.	Дата
Разраб.		Кырлан А.С.			04.11.26
Пров.					
ГИП					
Н. контр.					
Утв.					

ГД-2026-008-АИ

Квартира с кабинетом

Общая площадь 127,29* м² · * размеры со скана, не замерены (реестр — л. 6–8, К-1)

Дизайн-проект интерьера	Стадия	Лист	Листов
	РП	85	131

Схема расположения развёрток и узлов

М 1:75

Кырлан Александр Сергеевич

выпуск 04.11.2026 № 4177cbe7a3 · стр. 94 из 166

Развёртка стены А. Спальня (пом. 1)

Спальня (пом. 1) · вид изнутри помещения · размеры в мм, отметки в м

ПРЕДВАРИТЕЛЬНО · не для производства работ · открыто пунктов: 13 (реестр — л. 6–8)


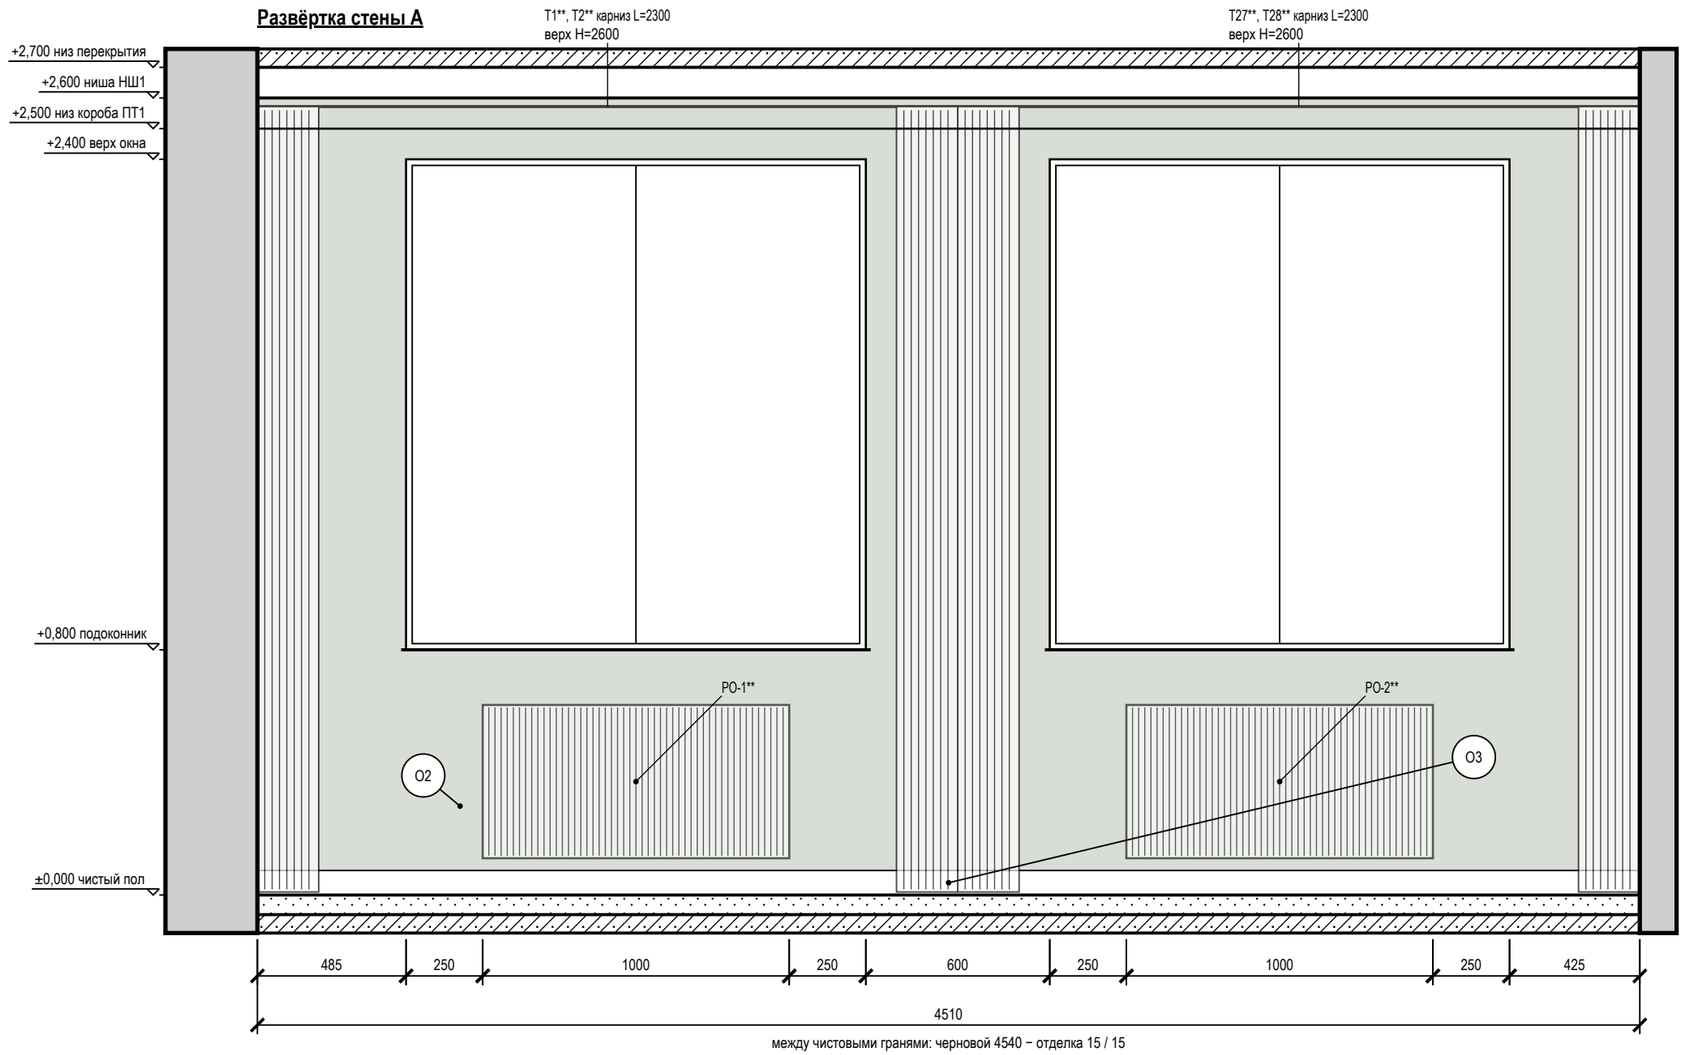


Схема развёрток (М 1:100)

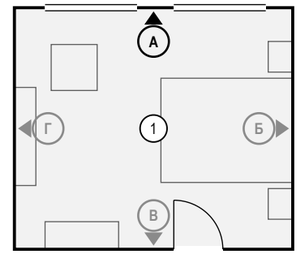

Условные обозначения

- мебель и приборы — фасад по расстановке (условно)
- карниз (шина) и шторы в собранном виде: марка Т, длина L, верх Н
- окно: проём, рама, подоконник
- радиатор отопления; марка — по плану отопления
- стены и перекрытия в сечении
- окраска: тон — цвет по коду производителя (условно)
- О1 — марка отделки по реестру отделки альбома
- А — марка развёртки: буква стены, стрелка — взгляд

Допущения и предложения на листе

Основа листа: размеры сняты с растрового плана заказчика с частичными размерами: рисунок не в масштабе, помещения выровнены по подписанным размерам мебели и проходов; контрольный обмер не выполнен (К-1); высота потолка 2700 мм принята: на плане заказчика её нет (К-2); толщины стен 300 / 120 мм приняты по плану заказчика, не замерены (К-1); разрешённая мощность 15 кВт принята по типовым ТУ для квартиры, ТУ заказчиком не переданы (К-4); подрайон климата не задан — принят не северный (жилые от 2,5 м) (К-6).

Знак «**» — предложение проектировщика, заказчиком не утверждено (согласовать с заказчиком): ИЗ-1: Т1, Т2 — Шина в нише штор (У1 +2,500, ниша +2,600 по всей стене А) — на окно 1 своя: 0…2300 по стене А (окно 500…2000: запас слева 500, справа 300 под пакет штор), вторая шина 2300…4600 — на окно 2 (Т27/Т28); вместе — длина ниши; Т27, Т28 — Шина на окно 2 в той же нише: 2300…4600 по стене А (окно 2600…4100: запас слева 300, справа 500); пара к Т1/Т2 на окне 1 — у обоих окон шторы, как на визуализации спальни; К-1: РО-1, РО-2 — прибор под окном по оси проёма, ширина ≈ 0,7 ширины окна — предложение ОВ (лист ОВ выводил его сам до, теперь он в данных — один источник для листа, мебели, DXF и IFC); стояки и подводки отопления не замерены, мощность — по теплотехническому расчёту ОВ.

См. лист открытых вопросов (лист 6, записи К-1, К-2, К-4, К-6; лист 7, запись ИЗ-1).

Примечания

1. Развёртки — вид на стену изнутри помещения, по часовой стрелке; расположение — на схеме листа и на листе 85; размеры — в мм по чистовым поверхностям; отметки — в м от ±0,000; высоты Н — от чистого пола помещения до оси изделия, у декора — до центра.
2. Схема мебели, приборов и декора не является технической документацией для производства мебели; габариты — по паспортам изделий.
3. Карнизы (шины) — по ведомости текстиля декоратора: длина L и верх Н на развёртке — те же числа, что в ведомости; крепление — до окраски потолка.
4. Потолок — у каждой стены свой, по плану потолков (НШ1, ПТ1); ступени — зоной, кромка короба перед нишей — тонкой линией; в поле потолка: ПТ2 +2,600.
5. Карниз Т1**, Т2**: по ведомости текстиля шина L=2300 мм, а от её начала до чистового угла стены — 2285 мм: шина не встаёт, длину согласовать с декоратором до заказа.
6. Карниз Т27**, Т28**: по ведомости текстиля шина L=2300 мм, а от её начала до чистового угла стены — 2225 мм: шина не встаёт, длину согласовать с декоратором до заказа.

1000 мм · печать 1:1

Изм.	Кол.уч	Лист	№ док.	Подп.	Дата
Разраб.		Кырлан А.С.			04.11.26
Пров.					
ГИП					
Н. контр.					
Утв.					

ГД-2026-008-АИ

Квартира с кабинетом

Общая площадь 127,29* м² · * размеры со скана, не замерены (реестр — л. 6–8, К-1)

Дизайн-проект интерьера

Стадия	Лист	Листов
РП	86	131

Развёртка стены А. Спальня (пом. 1)

М 1:20

Кырлан Александр Сергеевич

выпуск 04.11.2026 № 4177cbe7a3 · стр. 95 из 166

Развёртка стены Б. Спальня (пом. 1)

Спальня (пом. 1) · вид изнутри помещения · размеры в мм, отметки в м

ПРЕДВАРИТЕЛЬНО · не для производства работ · открыто пунктов: 13 (реестр — л. 6–8)

Развёртка стены Б


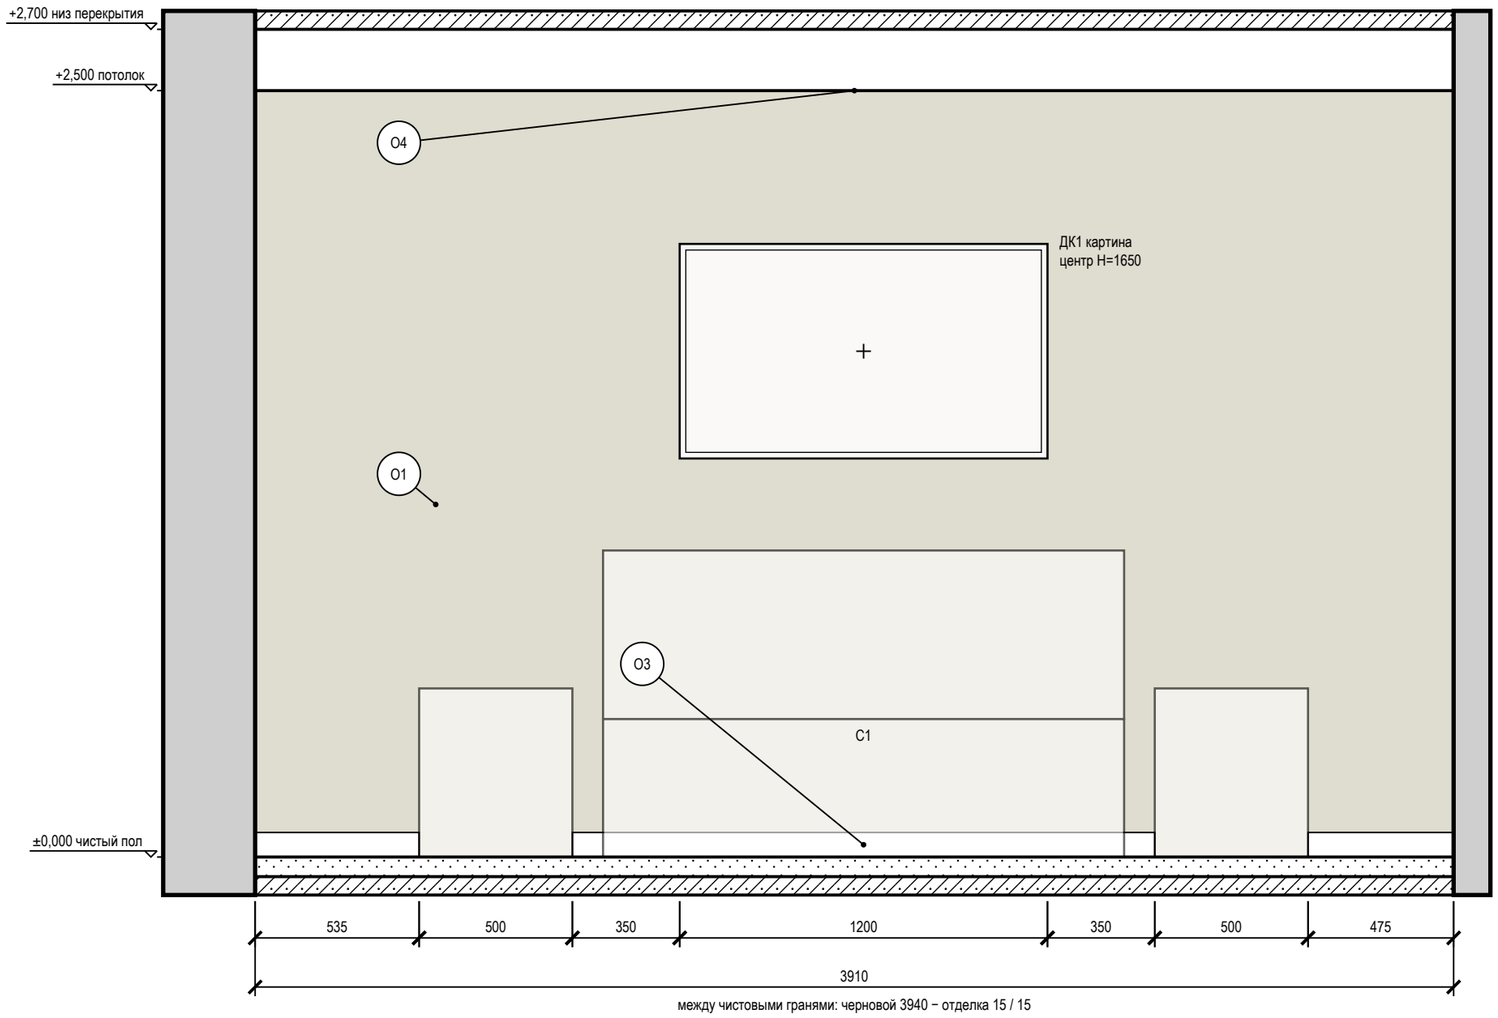


Схема развёрток (М 1:100)

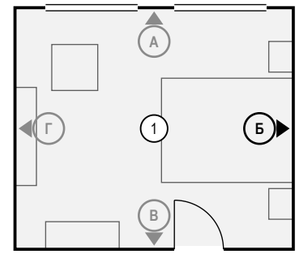

Условные обозначения

- мебель и приборы — фасад по расстановке (условно)
- картина (декор): марка Д, крест — центр, Н — высота центра, мм
- стены и перекрытия в сечении
- окраска: тон — цвет по коду производителя (условно)
- О1 — марка отделки по реестру отделки альбома
- А — марка развёртки: буква стены, стрелка — взгляд

Ведомость отделки (на листе)

Марка	Поверхность	Материал, изделие	Цвет, код	Кол.
О1	стены	окраска, Farrow & Ball Modern Emulsion, матовая, подготовка Q3	Farrow & Ball No. 15 «Bone — мягкий каменно-серый с зеленцой»	9,8 м²
О3	плинтус	плинтус МДФ, h 80 мм, аналог: плинтус МДФ под покраску 80×16	Farrow & Ball No. 15 «Bone — мягкий каменно-серый с зеленцой»	2,9 м
О4	потолок	окраска, Tikkurila Anti-Reflex 2, глубокоматовая, подготовка Q3	Tikkurila V503 «Winter»	17,9 м²

Допущения и предложения на листе

Основа листа: размеры сняты с растрового плана заказчика с частичными размерами: рисунок не в масштабе, помещения выровнены по подписанным размерам мебели и проходов; контрольный обмер не выполнен (К-1); высота потолка 2700 мм принята: на плане заказчика её нет (К-2); толщины стен 300 / 120 мм приняты по плану заказчика, не замерены (К-1); разрешённая мощность 15 кВт принята по типовым ТУ для квартиры, ТУ заказчиком не переданы (К-4); подрайон климата не задан — принят не северный (жилые от 2,5 м) (К-6).
См. лист открытых вопросов (лист 6, записи К-1, К-2, К-4, К-6).

Примечания

1. Развёртки — вид на стену изнутри помещения, по часовой стрелке; расположение — на схеме листа и на листе 85; размеры — в мм по чистовым поверхностям; отметки — в м от ±0,000; высоты Н — от чистого пола помещения до оси изделия, у декора — до центра.
2. Стена Б показана двумя видами: здесь — архитектурная развёртка (мебель, отделка, проёмы, высоты), электроточки и выводы ВК с привязками и таблицей — на листе 88 («Привязки»).
3. Схема мебели, приборов и декора не является технической документацией для производства мебели; габариты — по паспортам изделий.
4. Картины и зеркала крепить к основанию по паспорту изделия (закладные и анкеры — в перечне скрытых работ); крест — ось центра предмета.
5. Потолок — у каждой стены свой, по плану потолков (ПТ1); ступени — зоной, кромка короба перед нишей — тонкой линией; в поле потолка: ПТ2 +2,600.

1000 мм · печать 1:1

Изм.	Кол.уч	Лист	№ док.	Подп.	Дата
Разраб.		Кырлан А.С.			04.11.26
Пров.					
ГИП					
Н. контр.					
Утв.					

ГД-2026-008-АИ

Квартира с кабинетом

Общая площадь 127,29* м² · * размеры со скана, не замерены (реестр — л. 6–8, К-1)

Дизайн-проект интерьера

Стадия	Лист	Листов
РП	87	131

Развёртка стены Б. Спальня (пом. 1)

М 1:20

Кырлан Александр Сергеевич

выпуск 04.11.2026 № 4177cbe7a3 · стр. 96 из 166

Привязки электроточек, стена Б. Спальня (пом. 1)

Спальня (пом. 1) · вид изнутри помещения · привязки в мм, отметки в м · к развёртке на листе 87

ПРЕДВАРИТЕЛЬНО · не для производства работ · открыто пунктов: 13 (реестр — л. 6–8)

Развёртка стены Б: электроточки и выводы

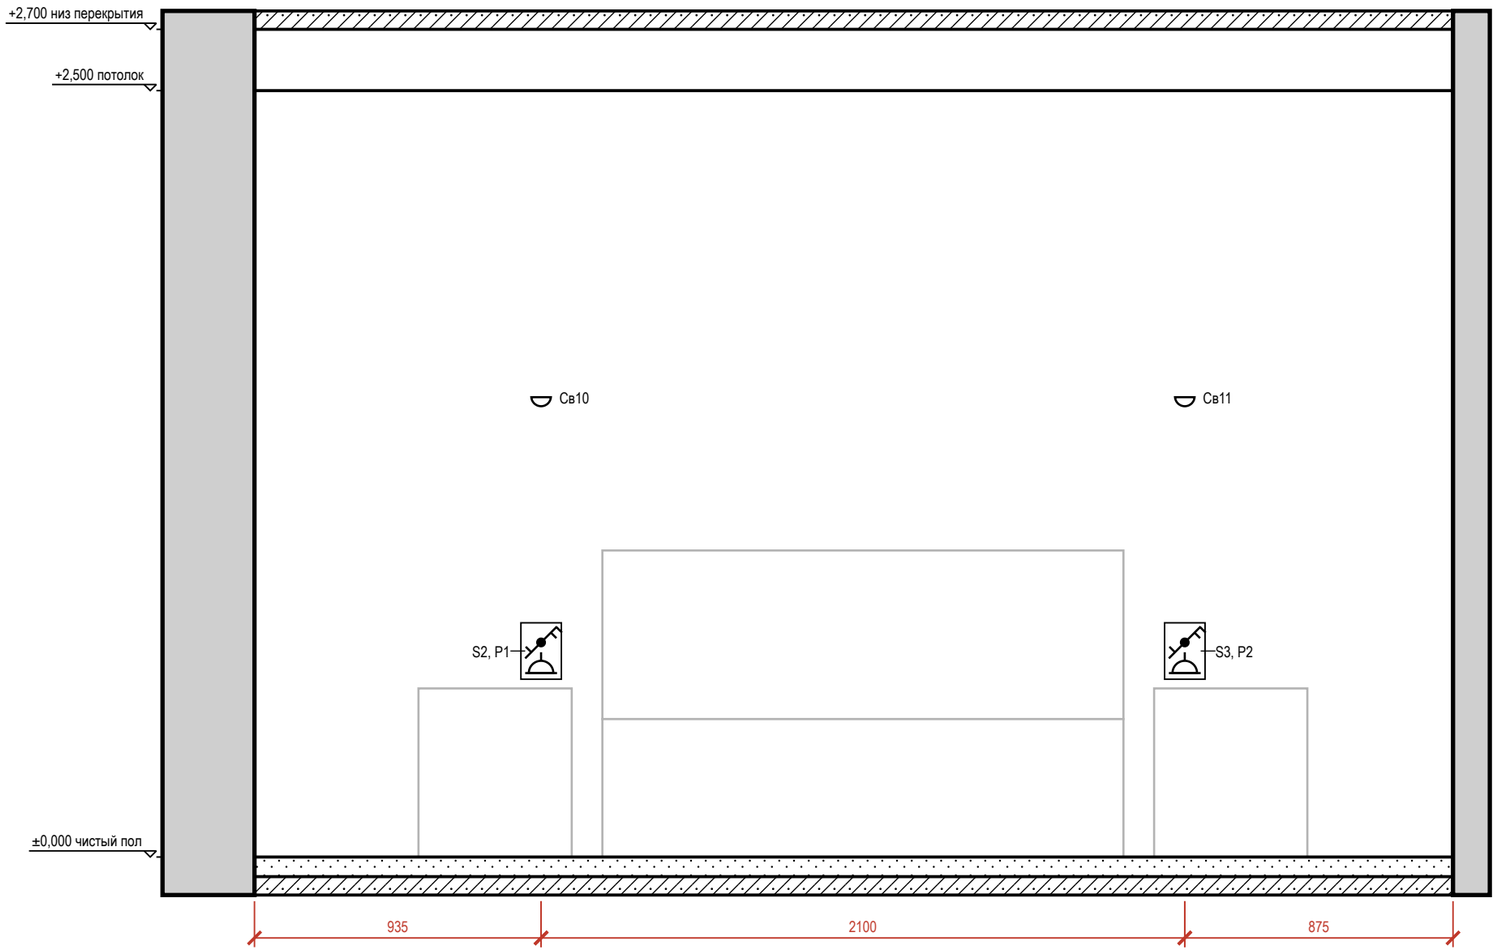



Таблица привязок электроточек и выводов

Марка	Назначение	От угла, мм	H от пола, мм	Примечание
P1	розетка: у кровати	935	600	гр. 4
S2	выключатель	935	700	гр. 1
Св10	светильник настенный	935	1500	гр. 1
P2	розетка: у кровати	3035	600	гр. 4
S3	выключатель	3035	700	гр. 1
Св11	светильник настенный	3035	1500	гр. 1

Условные обозначения

- розетка с заземляющим контактом; у знака — марка, ×N постов в рамке, гр. — группа щита, H — высота оси, мм
- выключатель одноклавишный
- выключатель двухклавишный (флажков — по числу клавиш)
- выключатель с проходной или перекрёстной клавишей (обратный флажок); тип клавиши — в подписи
- светильник настенный (бра), H — высота оси
- привязки точек и выводов от угла и от пола, мм
- A — марка развёртки: буква стены, стрелка — взгляд

Схема развёрток (М 1:100)

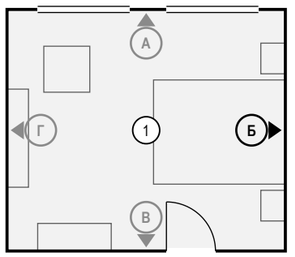

Примечания

1. Вид «Привязки» стены Б — электроточки и выводы ВК; архитектурная развёртка (мебель, отделка, проёмы, высоты) — на листе 87, расположение — на листе 85. Мебель и приборы — подложкой для ориентира; их марки и обозначения мебели, проёмов и стен — там же.
2. Привязки — в мм: по горизонтали от левого чистового угла стены до оси изделия, H — от чистого пола до оси; все точки — в таблице привязок. Красная цепочка — привязки по осям; точки ближе 120 мм одна к другой в цепочку не дробятся — их привязки только в таблице.
3. У знака — марка электроточки (P — розетка, S — выключатель, Св — светильник, ЭВ — вывод кабеля); посты в рамке и группа щита — в графе «Примечание»; группы по клавишам выключателя — на листе выключателей.

Допущения и предложения на листе

Основа листа: размеры сняты с растрового плана заказчика с частичными размерами: рисунок не в масштабе, помещения выровнены по подписанным размерам мебели и проходов; контрольный обмер не выполнен (К-1); высота потолка 2700 мм принята: на плане заказчика её нет (К-2); толщины стен 300 / 120 мм приняты по плану заказчика, не замерены (К-1); разрешённая мощность 15 кВт принята по типовым ТУ для квартиры, ТУ заказчиком не переданы (К-4); подрайон климата не задан — принят не северный (жилые от 2,5 м) (К-6). См. лист открытых вопросов (лист 6, записи К-1, К-2, К-4, К-6).

1000 мм · печать 1:1

Изм.	Кол.уч	Лист	№ док.	Подп.	Дата
Разраб.		Кырлан А.С.			04.11.26
Пров.					
ГИП					
Н. контр.					
Утв.					

ГД-2026-008-АИ

Квартира с кабинетом

Общая площадь 127,29* м² · * размеры со скана, не замерены (реестр — л. 6–8, К-1)

Дизайн-проект интерьера

Стадия	Лист	Листов
РП	88	131

Привязки электроточек, стена Б. Спальня (пом. 1)

М 1:20

Кырлан Александр Сергеевич


выпуск 04.11.2026 № 4177cbe7a3 · стр. 97 из 166

Развёртка стены В. Спальня (пом. 1)

Спальня (пом. 1) · вид изнутри помещения · размеры в мм, отметки в м


ПРЕДВАРИТЕЛЬНО · не для производства работ · открыто пунктов: 13 (реестр — л. 6–8)

Развёртка стены В

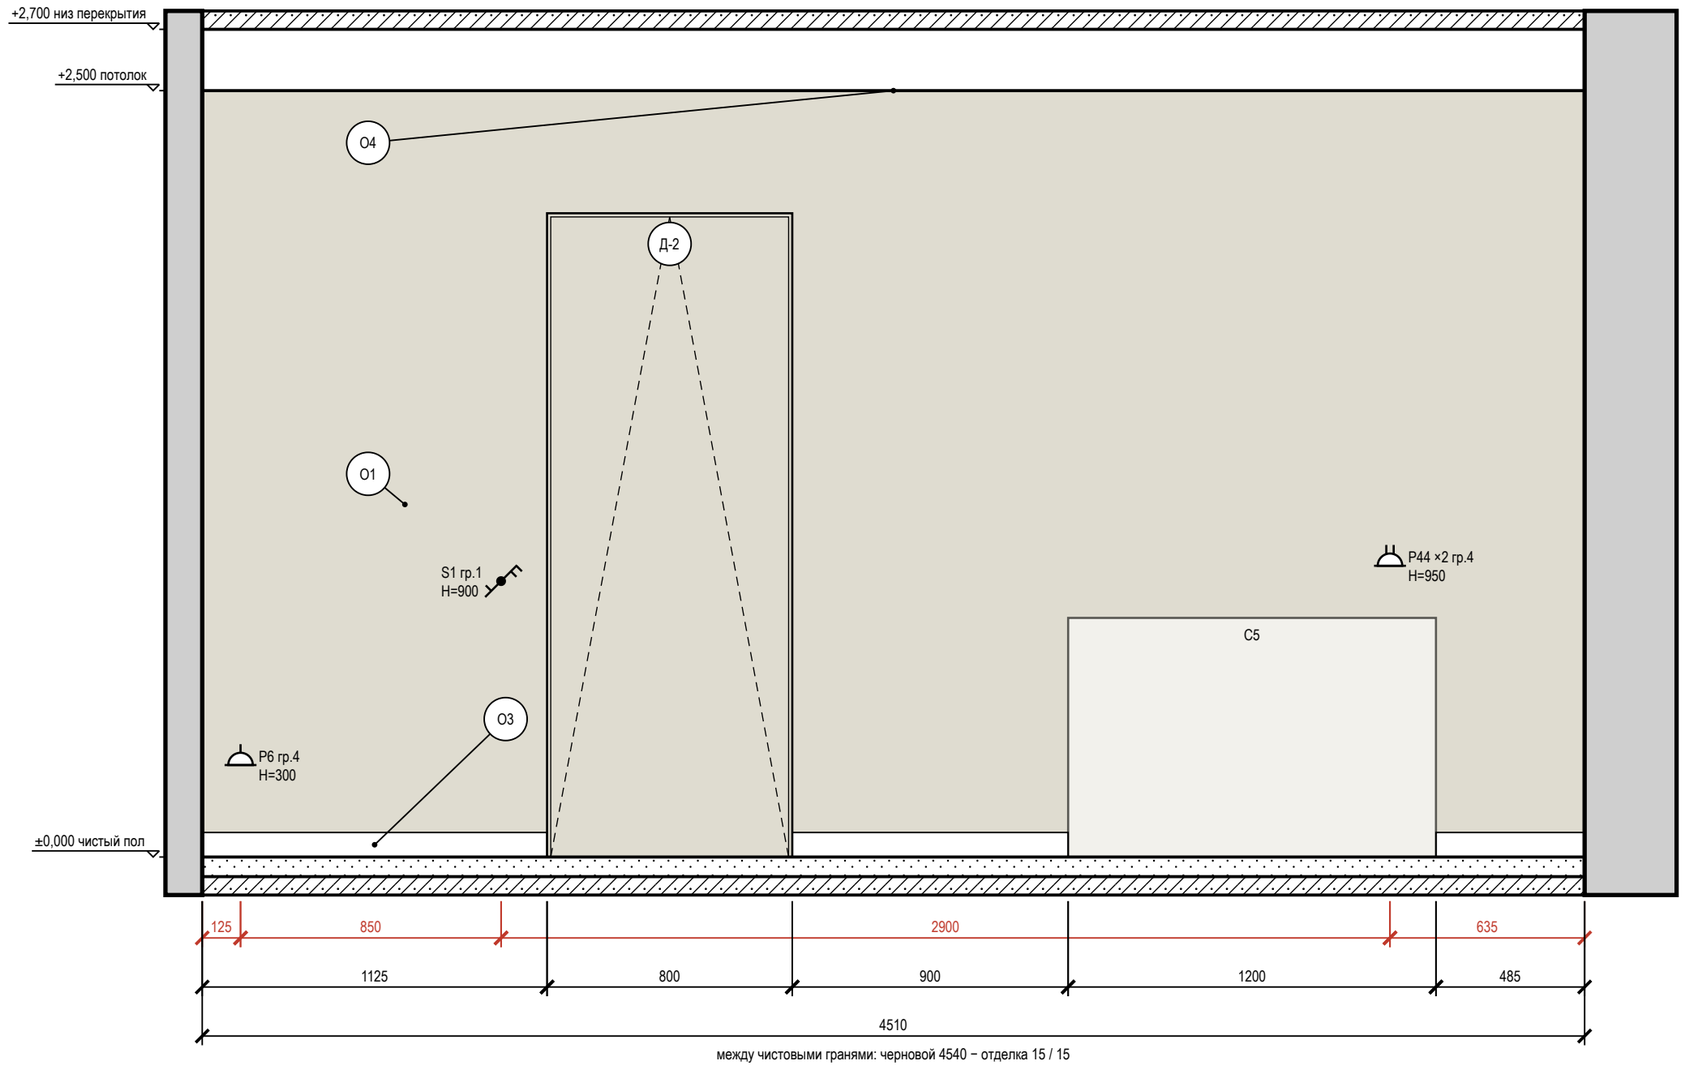

между чистовыми гранями: черновой 4540 − отделка 15 / 15

Схема развёрток (М 1:100)

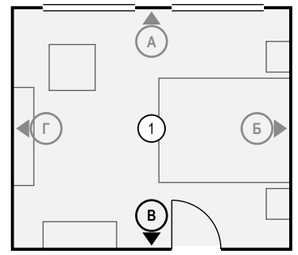

Условные обозначения

- розетка с заземляющим контактом; у знака — марка, ×N постов в рамке, гр. — группа щита, Н — высота оси, мм
- выключатель одноклавишный
- выключатель двухклавишный (флажков — по числу клавиш)
- выключатель с проходной или перекрёстной клавишей (обратный флажок); тип клавиши — в подписи
- привязки точек и выводов от угла и от пола, мм
- мебель и приборы — фасад по расстановке (условно)
- дверь скрытого монтажа: полотно в плоскости стены (узел — на листе узлов)
- стены и перекрытия в сечении
- окраска: тон — цвет по коду производителя (условно)
- О1 — марка отделки по реестру отделки альбома
- А — марка развёртки: буква стены, стрелка — взгляд

Допущения и предложения на листе

Основа листа: размеры сняты с растрового плана заказчика с частичными размерами: рисунок не в масштабе, помещения выровнены по подписанным размерам мебели и проходов; контрольный обмер не выполнен (К-1); высота потолка 2700 мм принята: на плане заказчика её нет (К-2); толщины стен 300 / 120 мм приняты по плану заказчика, не замерены (К-1); разрешённая мощность 15 кВт принята по типовым ТУ для квартиры, ТУ заказчиком не переданы (К-4); подрайон климата не задан — принят не северный (жилые от 2,5 м) (К-6).

См. лист открытых вопросов (лист 6, записи К-1, К-2, К-4, К-6).

Примечания

1. Развёртки — вид на стену изнутри помещения, по часовой стрелке; расположение — на схеме листа и на листе 85; размеры — в мм по чистовым поверхностям; отметки — в м от ±0,000; высоты Н — от чистого пола помещения до оси изделия, у декора — до центра.
2. Красная цепочка — привязки электроточек и выводов по осям от угла чистовых стен; высота Н — у знака, от чистого пола до оси; высоты мебели, проёмов и границ отделки — колонкой отметок слева. Стена с 5 и более точками или с мелкими звеньями привязок показана двумя видами: архитектурная развёртка (мебель, отделка, проёмы, высоты) и вид «Привязки» на отдельном листе — точки и выводы с марками, одна цепочка по осям и таблица привязок (каждая точка — строка).
3. У знака электроточки: марка (Р — розетка, S — выключатель, Св — светильник, ЭВ — вывод кабеля), ×N — число постов в рамке, гр. — группа щита, Н — высота оси от чистого пола, мм; группы по клавишам выключателя — на листе выключателей.
4. Схема мебели, приборов и декора не является технической документацией для производства мебели; габариты — по паспортам изделий.
5. Двери скрытого монтажа — полотно в плоскости стены, отделка стены по полотну, плинтус прерывается у короба (узел — на листе узлов).
6. Потолок — у каждой стены свой, по плану потолков (ПТ1); ступени — зоной, кромка короба перед нишей — тонкой линией; в поле потолка: ПТ2 +2,600.

1000 мм · печать 1:1

Изм.	Кол.уч	Лист	№ док.	Подп.	Дата
Разраб.		Кырлан А.С.			04.11.26
Пров.					
ГИП					
Н. контр.					
Утв.					

ГД-2026-008-АИ

Квартира с кабинетом

Общая площадь 127,29* м² · * размеры со скана, не замерены (реестр — л. 6–8, К-1)

Дизайн-проект интерьера

Стадия	Лист	Листов
РП	89	131

Развёртка стены В. Спальня (пом. 1)

М 1:20

Кырлан Александр Сергеевич


выпуск 04.11.2026 № 4177cbe7a3 · стр. 98 из 166

Развёртка стены Г. Спальня (пом. 1)

Спальня (пом. 1) · вид изнутри помещения · размеры в мм, отметки в м


ПРЕДВАРИТЕЛЬНО · не для производства работ · открыто пунктов: 13 (реестр — л. 6–8)

Развёртка стены Г

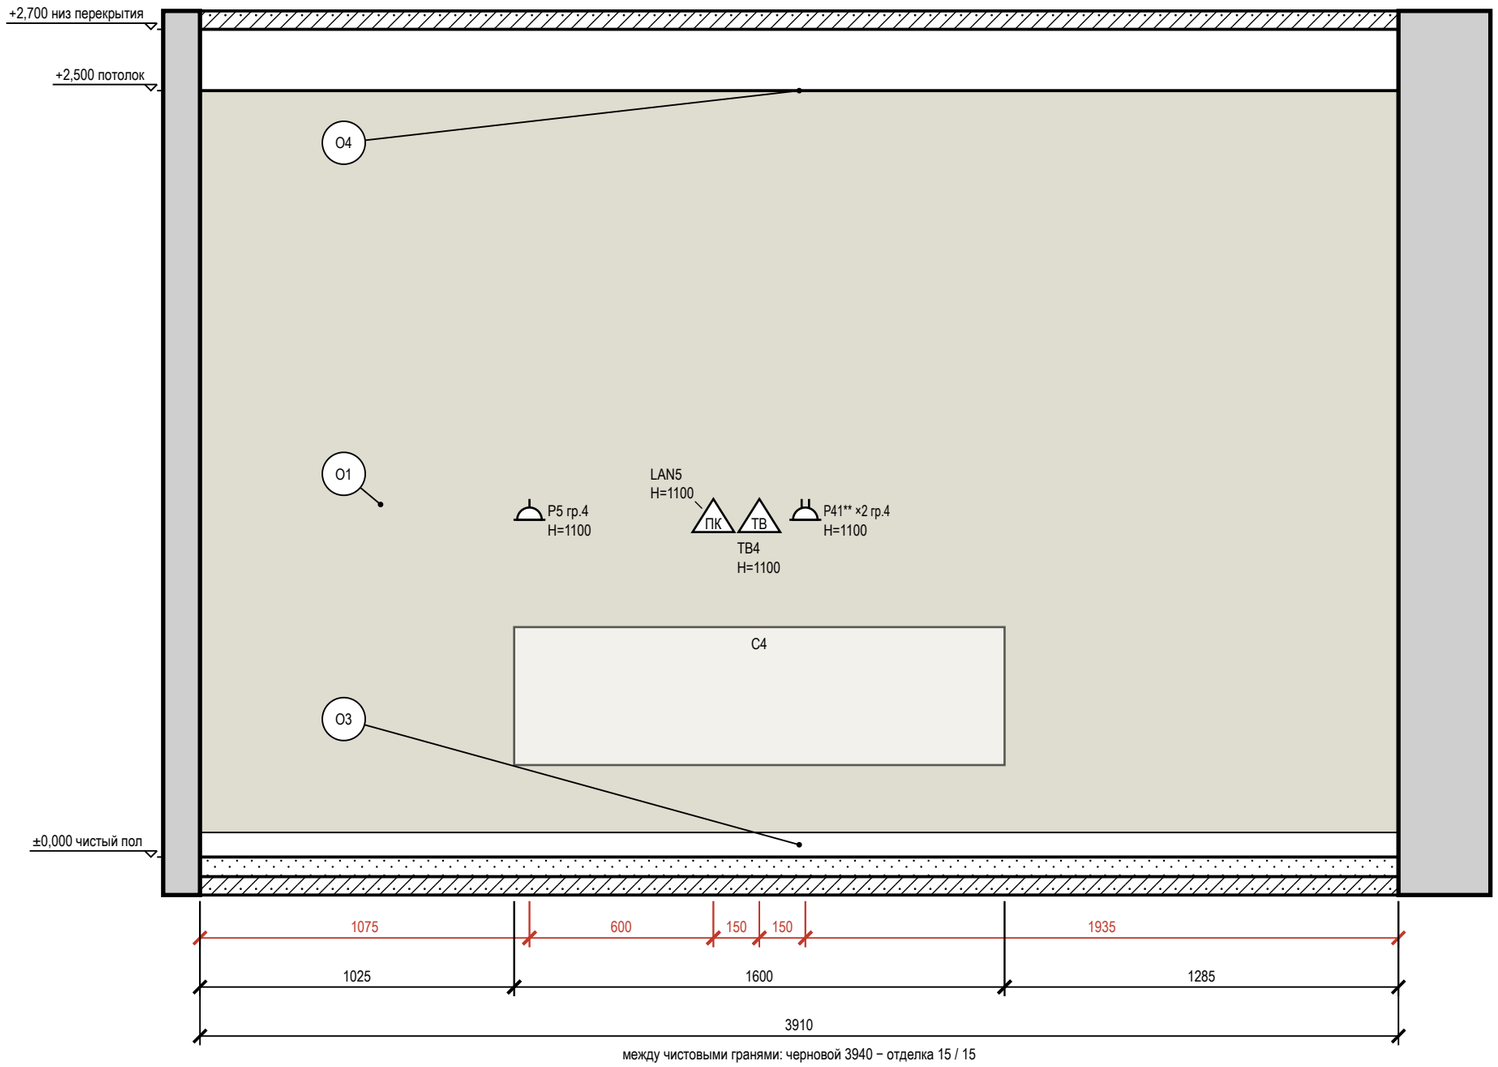

между чистовыми гранями: черновой 3940 − отделка 15 / 15

Схема развёрток (М 1:100)

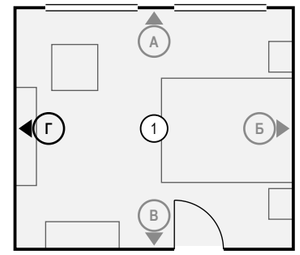

Условные обозначения

- розетка с заземляющим контактом; у знака — марка, ×N постов в рамке, гр. — группа щита, H — высота оси, мм
- ПК — розетка компьютерная RJ45
- ТВ — розетка телевизионная
- привязки точек и выводов от угла и от пола, мм
- мебель и приборы — фасад по расстановке (условно)
- стены и перекрытия в сечении
- окраска: тон — цвет по коду производителя (условно)
- О1 — марка отделки по реестру отделки альбома
- А — марка развёртки: буква стены, стрелка — взгляд

Ведомость отделки (на листе)

Марка	Поверхность	Материал, изделие	Цвет, код	Кол.
О1	стены	окраска, Farrow & Ball Modern Emulsion, матовая, подготовка Q3	Farrow & Ball No. 15 «Bone — мягкий каменно-серый с зеленцой»	9,8 м²
О3	плинтус	плинтус МДФ, h 80 мм, аналог: плинтус МДФ под покраску 80×16	Farrow & Ball No. 15 «Bone — мягкий каменно-серый с зеленцой»	3,9 м
О4	потолок	окраска, Tikkurila Anti-Reflex 2, глубокоматовая, подготовка Q3	Tikkurila V503 «Winter»	17,9 м²

Допущения и предложения на листе

Основа листа: размеры сняты с растрового плана заказчика с частичными размерами: рисунок не в масштабе, помещения выровнены по подписанным размерам мебели и проходов; контрольный обмер не выполнен (К-1); высота потолка 2700 мм принята: на плане заказчика её нет (К-2); толщины стен 300 / 120 мм приняты по плану заказчика, не замерены (К-1); разрешённая мощность 15 кВт принята по типовым ТУ для квартиры, ТУ заказчиком не переданы (К-4); подрайон климата не задан — принят не северный (жилые от 2,5 м) (К-6).

Знак «**» — предложение проектировщика, заказчиком не утверждено (согласовать с заказчиком): Р41 — высота 1100 мм выше нормы 1 м (ПУЭ 6.6.30) по назначению: питание ТВ — в ТВ-блоке над тумбой, за экраном.

См. лист открытых вопросов (лист 6, записи К-1, К-2, К-4, К-6).

Примечания

1. Развёртки — вид на стену изнутри помещения, по часовой стрелке; расположение — на схеме листа и на листе 85; размеры — в мм по чистовым поверхностям; отметки — в м от ±0,000; высоты H — от чистого пола помещения до оси изделия, у декора — до центра.
2. Красная цепочка — привязки электроточек и выводов по осям от угла чистовых стен; высота H — у знака, от чистого пола до оси; высоты мебели, проёмов и границ отделки — колонкой отметок слева. Стена с 5 и более точками или с мелкими звеньями привязок показана двумя видами: архитектурная развёртка (мебель, отделка, проёмы, высоты) и вид «Привязки» на отдельном листе — точки и выводы с марками, одна цепочка по осям и таблица привязок (каждая точка — строка).
3. У знака электроточки: марка (Р — розетка, S — выключатель, Св — светильник, ЭВ — вывод кабеля), ×N — число постов в рамке, гр. — группа щита, H — высота оси от чистого пола, мм; группы по клавишам выключателя — на листе выключателей.
4. Схема мебели, приборов и декора не является технической документацией для производства мебели; габариты — по паспортам изделий.
5. Потолок — у каждой стены свой, по плану потолков (ПТ1); ступени — зоной, кромка короба перед нишей — тонкой линией; в поле потолка: ПТ2 +2,600.

1000 мм · печать 1:1

Изм.	Кол.уч	Лист	№ док.	Подп.	Дата
Разраб.		Кырлан А.С.			04.11.26
Пров.					
ГИП					
Н. контр.					
Утв.					

ГД-2026-008-АИ

Квартира с кабинетом

Общая площадь 127,29* м² · * размеры со скана, не замерены (реестр — л. 6–8, К-1)

Дизайн-проект интерьера

Стадия	Лист	Листов
РП	90	131

Развёртка стены Г. Спальня (пом. 1)

М 1:20

Кырлан Александр Сергеевич


выпуск 04.11.2026 № 4177cbe7a3 · стр. 99 из 166

Развёртки стен А, Б. Гардеробная-постирочная (пом. 2)

Гардеробная-постирочная (пом. 2) · вид изнутри помещения · размеры в мм, отметки в м


ПРЕДВАРИТЕЛЬНО · не для производства работ · открыто пунктов: 13 (реестр — л. 6–8)

Развёртка стены А

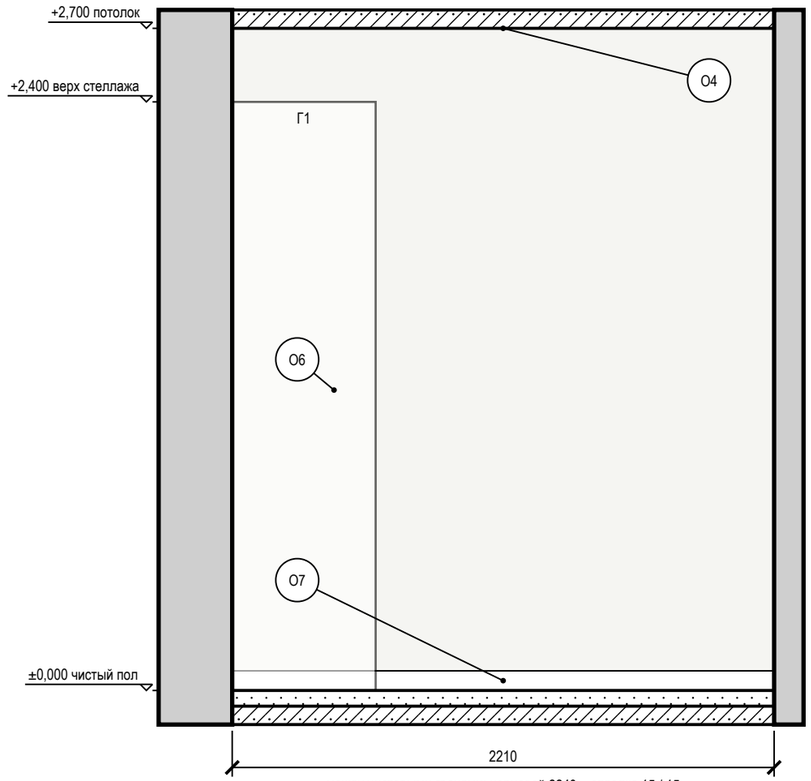


между чистовыми гранями: черновой 2240 − отделка 15 / 15

Развёртка стены Б

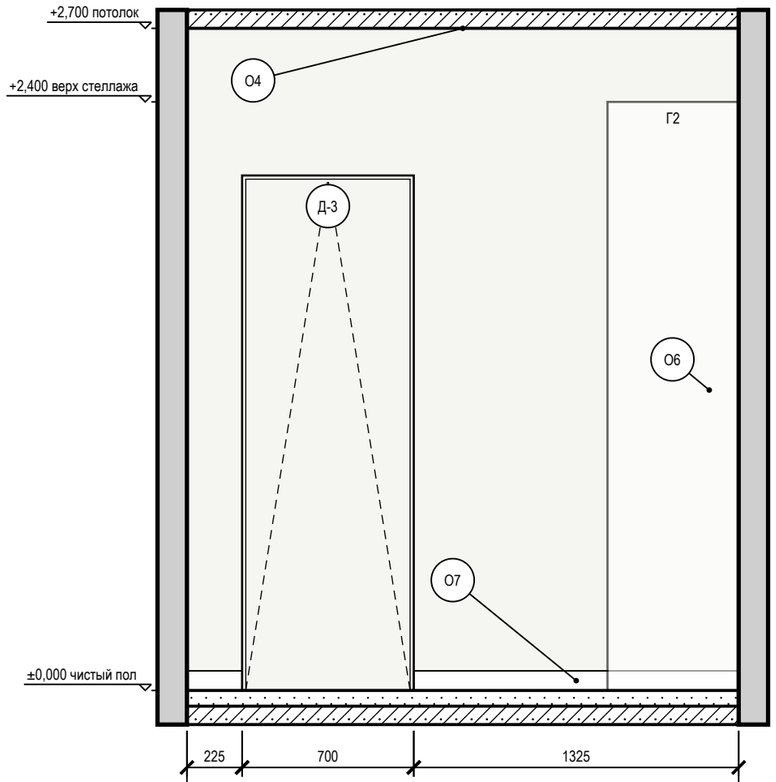

между чистовыми гранями: черновой 2280 − отделка 15 / 15

Схема развёрток (М 1:100)

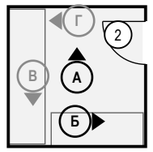

Условные обозначения

- мебель и приборы — фасад по расстановке (условно)
- дверь скрытого монтажа: полотно в плоскости стены (узел — на листе узлов)
- стены и перекрытия в сечении
- окраска: тон — цвет по коду производителя (условно)
- О1 — марка отделки по реестру отделки альбома
- А — марка развёртки: буква стены, стрелка — взгляд

Ведомость отделки (на листе)

Марка	Поверхность	Материал, изделие	Цвет, код	Кол.
О4	потолок	окраска, Tikkurila Anti-Reflex 2, глубокоматовая, подготовка Q3	Tikkurila V503 «Winter»	5,1 м²
О6	стены	окраска, Tikkurila Harmony, матовая, подготовка Q3	Tikkurila V503 «Winter»	10,6 м²
О7	плинтус	плинтус МДФ, h 80 мм, аналог: плинтус МДФ под покраску 80×16	Tikkurila V503 «Winter»	3,8 м

Примечания

1. Развёртки — вид на стену изнутри помещения, по часовой стрелке; расположение — на схеме листа и на листе 85; размеры — в мм по чистовым поверхностям; отметки — в м от ±0,000; высоты Н — от чистого пола помещения до оси изделия, у декора — до центра.
2. Схема мебели, приборов и декора не является технической документацией для производства мебели; габариты — по паспортам изделий.
3. Двери скрытого монтажа — полотно в плоскости стены, отделка стены по полотну, плинтус прерывается у короба (узел — на листе узлов).

Допущения и предложения на листе

Основа листа: размеры сняты с растрового плана заказчика с частичными размерами: рисунок не в масштабе, помещения выровнены по подписанным размерам мебели и проходов; контрольный обмер не выполнен (К-1); высота потолка 2700 мм принята: на плане заказчика её нет (К-2); толщины стен 300 / 120 мм приняты по плану заказчика, не замерены (К-1); разрешённая мощность 15 кВт принята по типовым ТУ для квартиры, ТУ заказчиком не переданы (К-4); подрайон климата не задан — принят не северный (жилые от 2,5 м) (К-6).
См. лист открытых вопросов (лист 6, записи К-1, К-2, К-4, К-6).

1000 мм · печать 1:1

Изм.	Кол.уч	Лист	№ док.	Подп.	Дата
Разраб.		Кырлан А.С.			04.11.26
Пров.					
ГИП					
Н. контр.					
Утв.					

ГД-2026-008-АИ

Квартира с кабинетом

Общая площадь 127,29* м² · * размеры со скана, не замерены (реестр — л. 6–8, К-1)

Дизайн-проект интерьера

Стадия	Лист	Листов
РП	91	131

Развёртки стен А, Б. Гардеробная-постирочная (пом. 2)

М 1:25

Кырлан Александр Сергеевич


выпуск 04.11.2026 № 4177cbe7a3 · стр. 100 из 166

Развёртки стен В, Г. Гардеробная-постирочная (пом. 2)

Гардеробная-постирочная (пом. 2) · вид изнутри помещения · размеры в мм, отметки в м


ПРЕДВАРИТЕЛЬНО · не для производства работ · открыто пунктов: 13 (реестр — л. 6–8)

Развёртка стены В

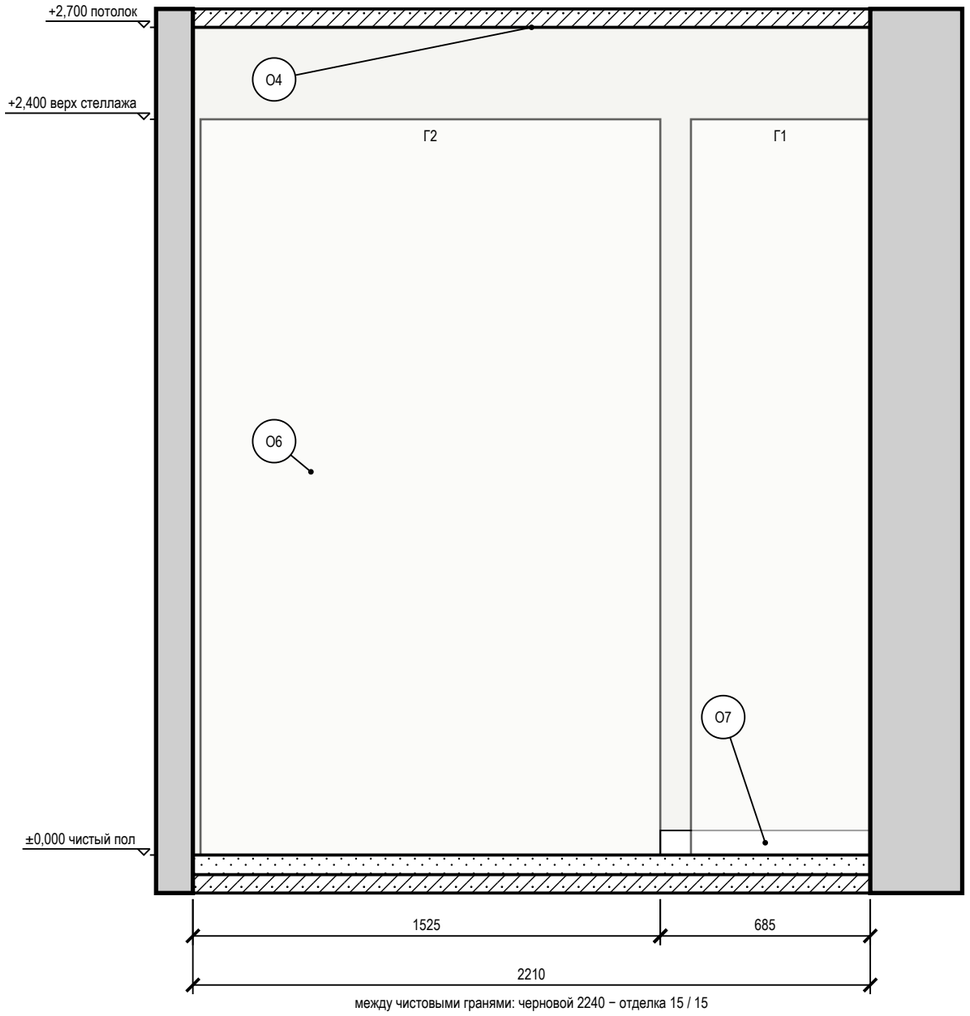


между чистовыми гранями: черновой 2240 − отделка 15 / 15

Развёртка стены Г

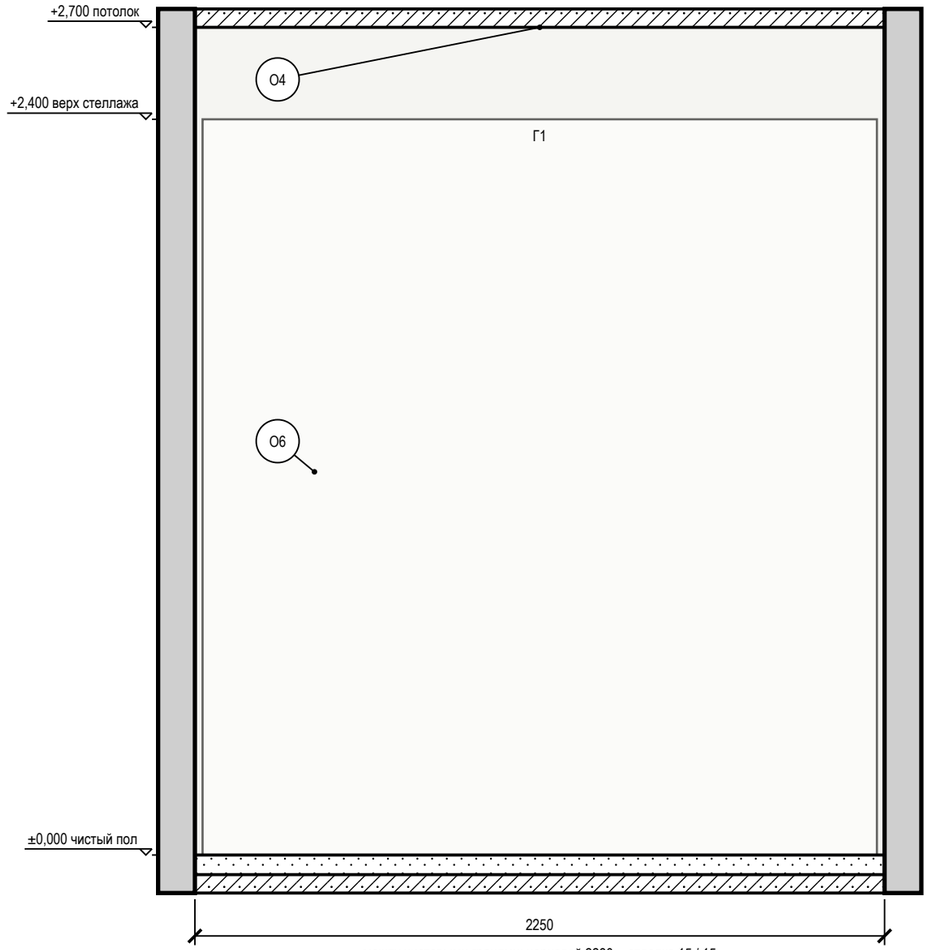

между чистовыми гранями: черновой 2280 − отделка 15 / 15

Схема развёрток (М 1:100)

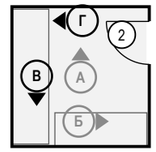

Условные обозначения

- мебель и приборы — фасад по расстановке (условно)
- стены и перекрытия в сечении
- окраска: тон — цвет по коду производителя (условно)
- О1 — марка отделки по реестру отделки альбома
- А — марка развёртки: буква стены, стрелка — взгляд

Примечания

1. Развёртки — вид на стену изнутри помещения, по часовой стрелке; расположение — на схеме листа и на листе 85; размеры — в мм по чистовым поверхностям; отметки — в м от ±0,000; высоты Н — от чистого пола помещения до оси изделия, у декора — до центра.
2. Схема мебели, приборов и декора не является технической документацией для производства мебели; габариты — по паспортам изделий.

Допущения и предложения на листе

Основа листа: размеры сняты с растрового плана заказчика с частичными размерами: рисунок не в масштабе, помещения выровнены по подписанным размерам мебели и проходов; контрольный обмер не выполнен (К-1); высота потолка 2700 мм принята: на плане заказчика её нет (К-2); толщины стен 300 / 120 мм приняты по плану заказчика, не замерены (К-1); разрешённая мощность 15 кВт принята по типовым ТУ для квартиры, ТУ заказчиком не переданы (К-4); подрайон климата не задан — принят не северный (жилые от 2,5 м) (К-6). См. лист открытых вопросов (лист 6, записи К-1, К-2, К-4, К-6).

1000 мм · печать 1:1

Изм.	Кол.уч	Лист	№ док.	Подп.	Дата
Разраб.		Кырлан А.С.			04.11.26
Пров.					
ГИП					
Н. контр.					
Утв.					

ГД-2026-008-АИ

Квартира с кабинетом

Общая площадь 127,29* м² · * размеры со скана, не замерены (реестр — л. 6–8, К-1)

Дизайн-проект интерьера

Стадия	Лист	Листов
РП	92	131

Развёртки стен В, Г. Гардеробная-постирочная (пом. 2)

М 1:20

Кырлан Александр Сергеевич

выпуск 04.11.2026 № 4177cbe7a3 · стр. 101 из 166

Развёртка стены А. Кабинет (пом. 3)

Кабинет (пом. 3) · вид изнутри помещения · размеры в мм, отметки в м

ПРЕДВАРИТЕЛЬНО · не для производства работ · открыто пунктов: 13 (реестр — л. 6–8)

Развёртка стены А


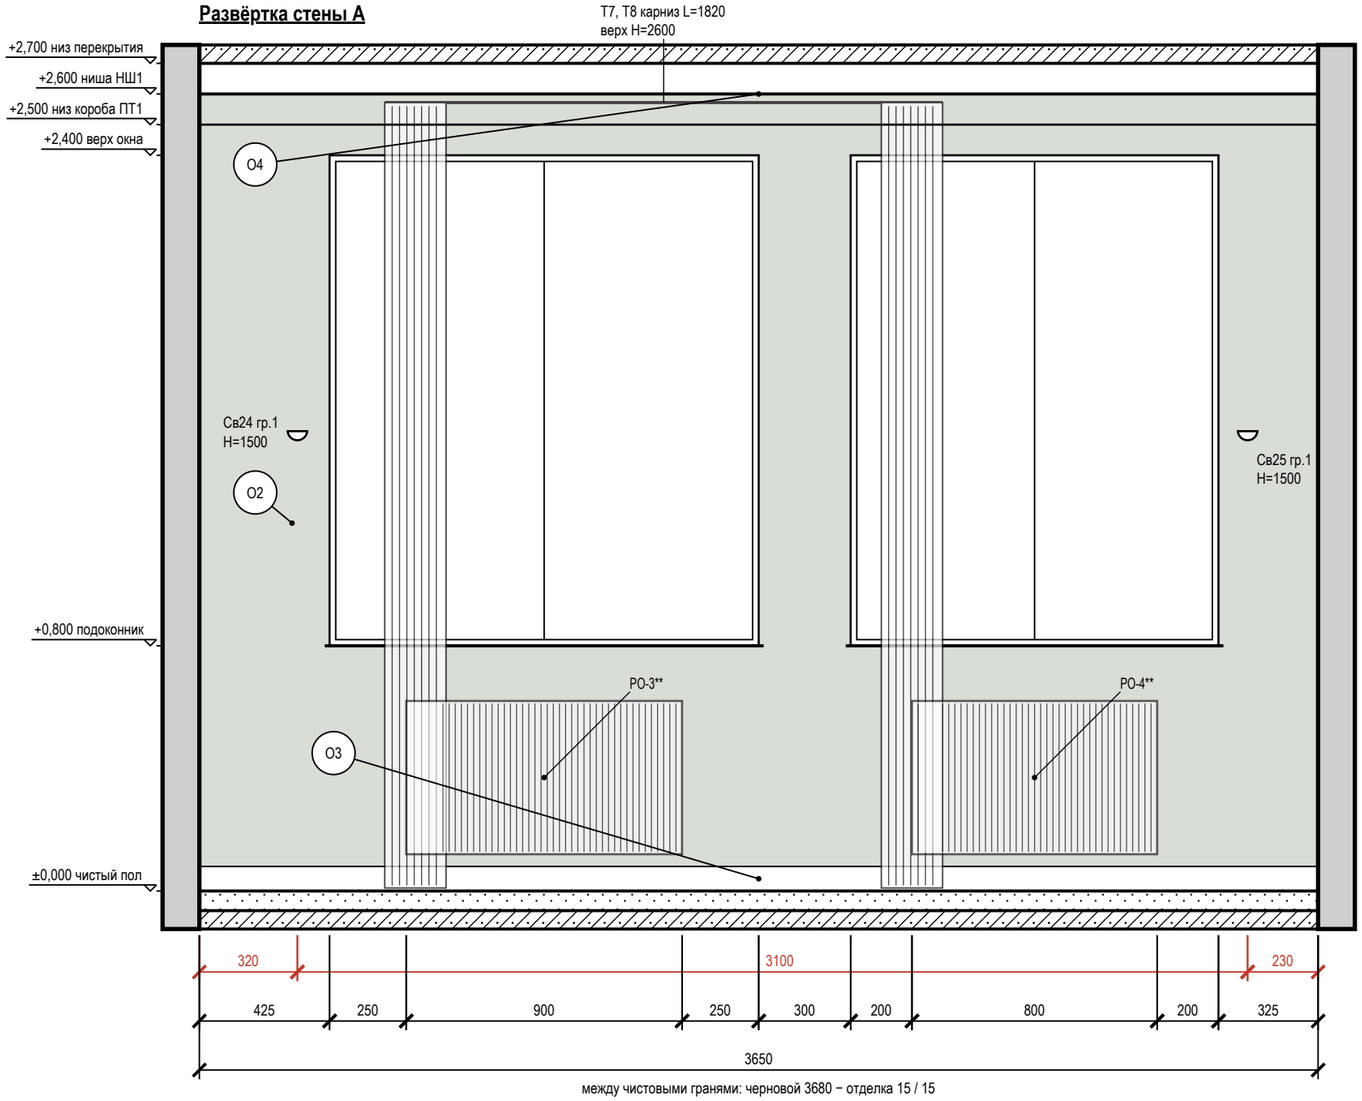


Схема развёрток (М 1:100)

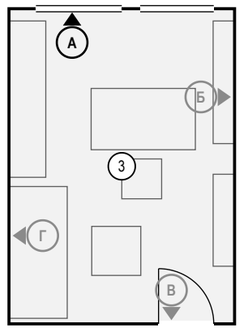

Условные обозначения

- светильник настенный (бра), H — высота оси
- привязки точек и выводов от угла и от пола, мм
- мебель и приборы — фасад по расстановке (условно)
- карниз (шина) и шторы в собранном виде: марка Т, длина L, верх H
- окно: проём, рама, подоконник
- радиатор отопления; марка — по плану отопления
- стены и перекрытия в сечении
- окраска: тон — цвет по коду производителя (условно)
- О1 — марка отделки по реестру отделки альбома
- А — марка развёртки: буква стены, стрелка — взгляд

Ведомость отделки (на листе)

Марка	Поверхность	Материал, изделие	Цвет, код	Кол.
О2	акцентная стена	окраска, Farrow & Ball Modern Emulsion, матовая, подготовка Q3	Farrow & Ball No. 34 «Calke Green традиционный шалфей»	5,3 м²
О3	плинтус	плинтус МДФ, h 80 мм, аналог: плинтус МДФ под покраску 80×16	Farrow & Ball No. 15 «Bone — мягкий каменно-серый с зеленцой»	3,6 м
О4	потолок	окраска, Tikkurila Anti-Reflex 2, глубокоматовая, подготовка Q3	Tikkurila V503 «Winter»	18,9 м²

Допущения и предложения на листе

Основа листа: размеры сняты с растрового плана заказчика с частичными размерами: рисунок не в масштабе, помещения выровнены по подписанным размерам мебели и проходов; контрольный обмер не выполнен (К-1); высота потолка 2700 мм принята: на плане заказчика её нет (К-2); толщины стен 300 / 120 мм приняты по плану заказчика, не замерены (К-1); разрешённая мощность 15 кВт принята по типовым ТУ для квартиры, ТУ заказчиком не переданы (К-4); подрайон климата не задан — принят не северный (жилые от 2,5 м) (К-6).

Знак «**» — предложение проектировщика, заказчиком не утверждено (согласовать с заказчиком): К-1: РО-3, РО-4 — прибор под окном по оси проёма, ширина ≈ 0,7 ширины окна — предложение ОВ (лист ОВ выводил его сам до, теперь он в данных — один источник для листа, мебели, DXF и IFC); стояки и подводки отопления не замерены, мощность — по теплотехническому расчёту ОВ. См. лист открытых вопросов (лист 6, записи К-1, К-2, К-4, К-6).

Примечания

1. Развёртки — вид на стену изнутри помещения, по часовой стрелке; расположение — на схеме листа и на листе 85; размеры — в мм по чистовым поверхностям; отметки — в м от ±0,000; высоты H — от чистого пола помещения до оси изделия, у декора — до центра.
2. Красная цепочка — привязки электроточек и выводов по осям от угла чистовых стен; высота H — у знака, от чистого пола до оси; высоты мебели, проёмов и границ отделки — колонкой отметок слева. Стена с 5 и более точками или с мелкими звеньями привязок показана двумя видами: архитектурная развёртка (мебель, отделка, проёмы, высоты) и вид «Привязки» на отдельном листе — точки и выводы с марками, одна цепочка по осям и таблица привязок (каждая точка — строка).
3. У знака электроточки: марка (Р — розетка, S — выключатель, Св — светильник, ЭВ — вывод кабеля), ×N — число постов в рамке, гр. — группа щита, H — высота оси от чистого пола, мм; группы по клавишам выключателя — на листе выключателей.
4. Схема мебели, приборов и декора не является технической документацией для производства мебели; габариты — по паспортам изделий.
5. Карнизы (шины) — по ведомости текстиля декоратора: длина L и верх H на развёртке — те же числа, что в ведомости; крепление — до окраски потолка.
6. Потолок — у каждой стены свой, по плану потолков (НШ1, ПТ1); ступени — зоной, кромка короба перед нишей — тонкой линией; в поле потолка: ПТ2 +2,600.
7. Линии узора (швы плитки, складки штор, рёбра радиаторов) прерываются у знаков и выносок — просвет между линиями не менее 0,7 мм.

1000 мм · печать 1:1

Изм.	Кол.уч	Лист	№ док.	Подп.	Дата
Разраб.		Кырлан А.С.			04.11.26
Пров.					
ГИП					
Н. контр.					
Утв.					

ГД-2026-008-АИ

Квартира с кабинетом

Общая площадь 127,29* м² · * размеры со скана, не замерены (реестр — л. 6–8, К-1)

Дизайн-проект интерьера

Стадия	Лист	Листов
РП	93	131

Развёртка стены А. Кабинет (пом. 3)

М 1:20

Кырлан Александр Сергеевич


выпуск 04.11.2026 № 4177cbe7a3 · стр. 102 из 166

Развёртка стены Б. Кабинет (пом. 3)

Кабинет (пом. 3) · вид изнутри помещения · размеры в мм, отметки в м


ПРЕДВАРИТЕЛЬНО · не для производства работ · открыто пунктов: 13 (реестр — л. 6–8)

Развёртка стены Б

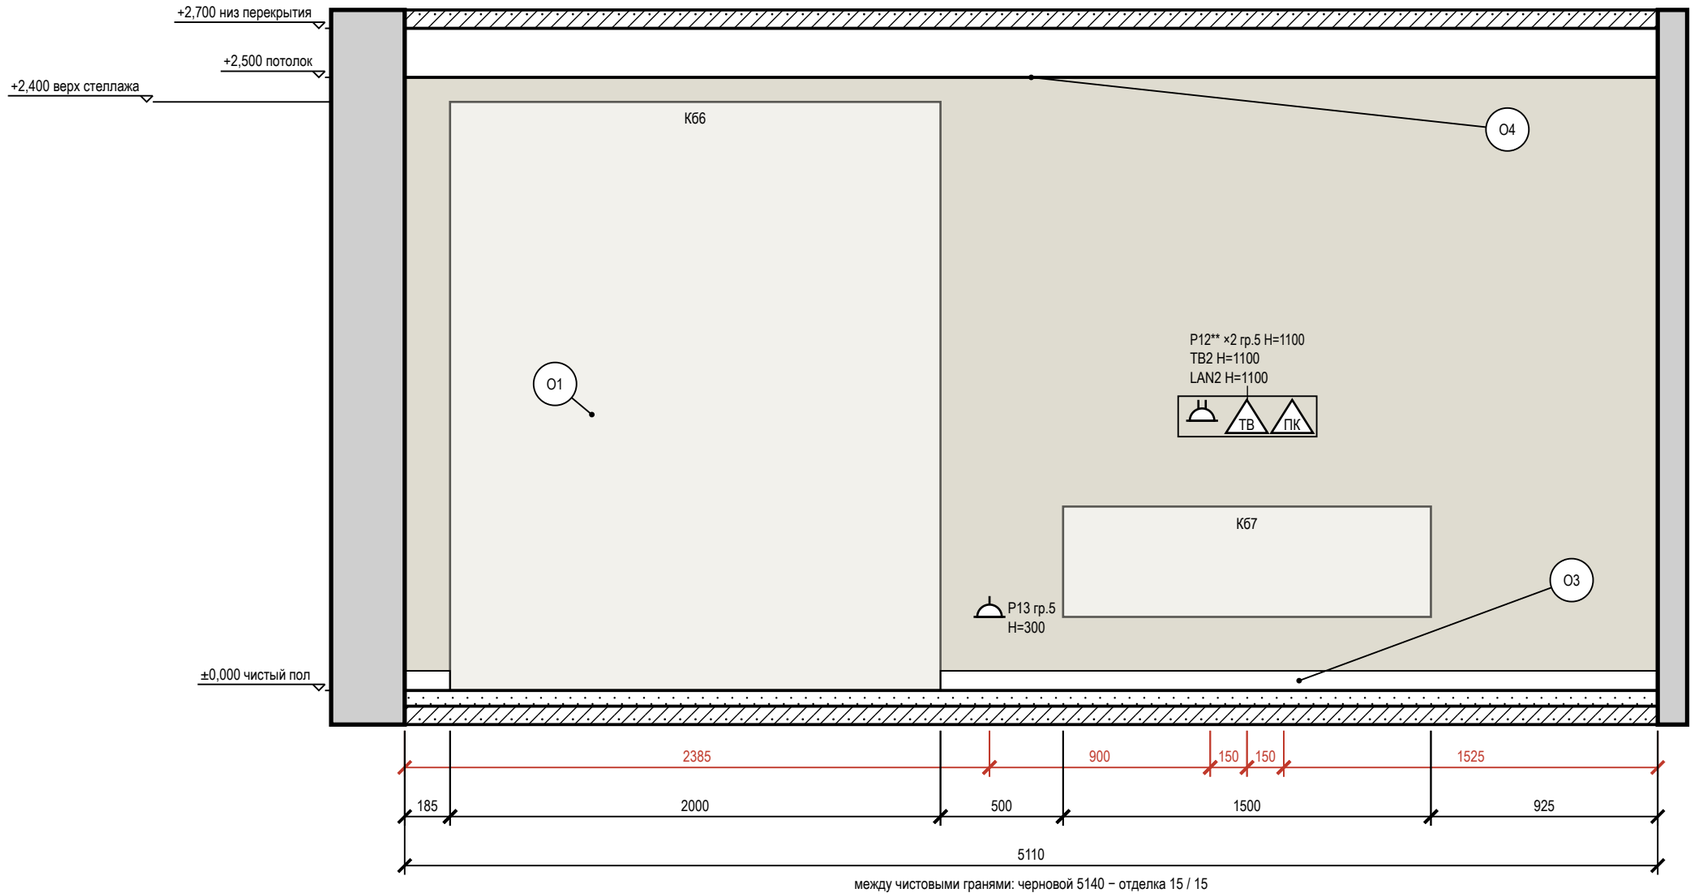

между чистовыми гранями: черновой 5140 − отделка 15 / 15

Схема развёрток (М 1:100)

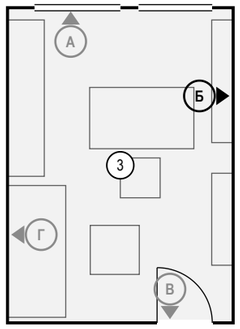

Условные обозначения

- розетка с заземляющим контактом; у знака — марка, ×N постов в рамке, гр. — группа щита, Н — высота оси, мм
- ПК — розетка компьютерная RJ45
- ТВ — розетка телевизионная
- привязки точек и выводов от угла и от пола, мм
- мебель и приборы — фасад по расстановке (условно)
- стены и перекрытия в сечении
- окраска: тон — цвет по коду производителя (условно)
- О1 — марка отделки по реестру отделки альбома
- А — марка развёртки: буква стены, стрелка — взгляд

Ведомость отделки (на листе)

Марка	Поверхность	Материал, изделие	Цвет, код	Кол.
О1	стены	окраска, Farrow & Ball Modern Emulsion, матовая, подготовка Q3	Farrow & Ball No. 15 «Bone — мягкий каменно-серый с зеленцой»	12,8 м²
О3	плинтус	плинтус МДФ, h 80 мм, аналог: плинтус МДФ под покраску 80×16	Farrow & Ball No. 15 «Bone — мягкий каменно-серый с зеленцой»	3,1 м
О4	потолок	окраска, Tikkurila Anti-Reflex 2, глубокоматовая, подготовка Q3	Tikkurila V503 «Winter»	18,9 м²

Допущения и предложения на листе

Основа листа: размеры сняты с растрового плана заказчика с частичными размерами: рисунок не в масштабе, помещения выровнены по подписанным размерам мебели и проходов; контрольный обмер не выполнен (К-1); высота потолка 2700 мм принята: на плане заказчика её нет (К-2); толщины стен 300 / 120 мм приняты по плану заказчика, не замерены (К-1); разрешённая мощность 15 кВт принята по типовым ТУ для квартиры, ТУ заказчиком не переданы (К-4); подрайон климата не задан — принят не северный (жилые от 2,5 м) (К-6).
Знак «**» — предложение проектировщика, заказчиком не утверждено (согласовать с заказчиком): Р12 — высота 1100 мм выше нормы 1 м (ПУЭ 6.6.30) по назначению: питание ТВ — в ТВ-блоке над тумбой, за экраном.
См. лист открытых вопросов (лист 6, записи К-1, К-2, К-4, К-6).

Примечания

1. Развёртки — вид на стену изнутри помещения, по часовой стрелке; расположение — на схеме листа и на листе 85; размеры — в мм по чистовым поверхностям; отметки — в м от ±0,000; высоты Н — от чистого пола помещения до оси изделия, у декора — до центра.
2. Красная цепочка — привязки электроточек и выводов по осям от угла чистовых стен; высота Н — у знака, от чистого пола до оси; высоты мебели, проёмов и границ отделки — колонкой отметок слева. Стена с 5 и более точками или с мелкими звеньями привязок показана двумя видами: архитектурная развёртка (мебель, отделка, проёмы, высоты) и вид «Привязки» на отдельном листе — точки и выводы с марками, одна цепочка по осям и таблица привязок (каждая точка — строка).
3. У знака электроточки: марка (Р — розетка, S — выключатель, Св — светильник, ЭВ — вывод кабеля), ×N — число постов в рамке, гр. — группа щита, Н — высота оси от чистого пола, мм; группы по клавишам выключателя — на листе выключателей.
4. Схема мебели, приборов и декора не является технической документацией для производства мебели; габариты — по паспортам изделий.
5. Потолок — у каждой стены свой, по плану потолков (ПТ1); ступени — зоной, кромка короба перед нишей — тонкой линией; в поле потолка: ПТ2 +2,600.

1000 мм · печать 1:1

Изм.	Кол.уч	Лист	№ док.	Подп.	Дата
Разраб.		Кырлан А.С.			04.11.26
Пров.					
ГИП					
Н. контр.					
Утв.					

ГД-2026-008-АИ

Квартира с кабинетом

Общая площадь 127,29* м² · * размеры со скана, не замерены (реестр — л. 6–8, К-1)

Дизайн-проект интерьера

Стадия	Лист	Листов
РП	94	131

Развёртка стены Б. Кабинет (пом. 3)

М 1:25

Кырлан Александр Сергеевич

выпуск 04.11.2026 № 4177cbe7a3 · стр. 103 из 166

Развёртка стены В. Кабинет (пом. 3)

Кабинет (пом. 3) · вид изнутри помещения · размеры в мм, отметки в м

ПРЕДВАРИТЕЛЬНО · не для производства работ · открыто пунктов: 13 (реестр — л. 6–8)

Развёртка стены В


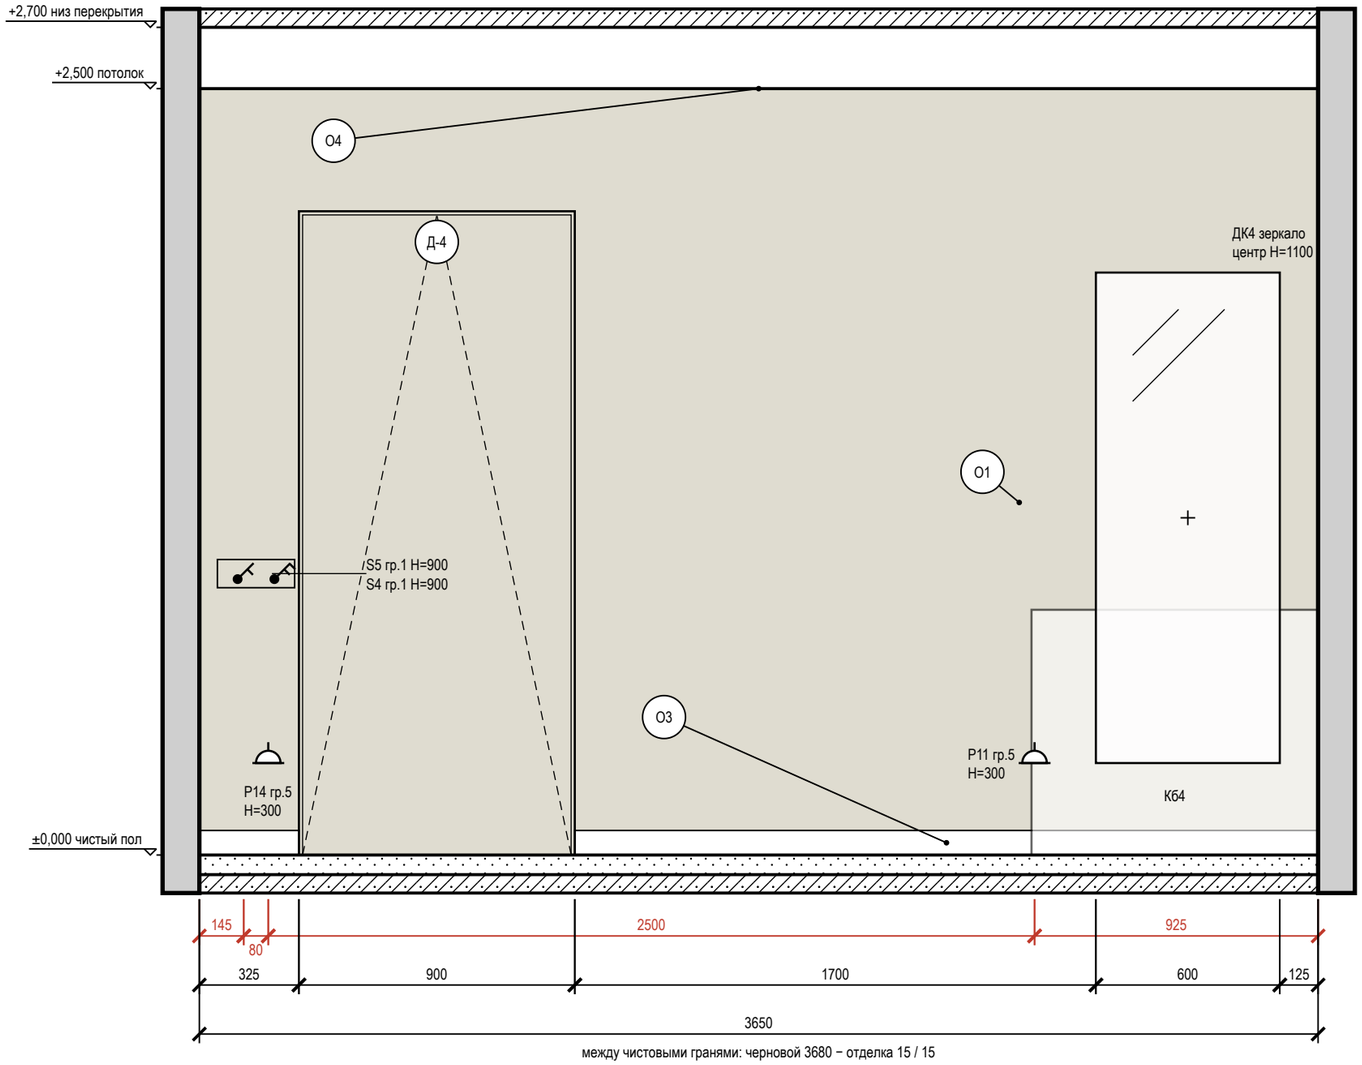


Схема развёрток (М 1:100)

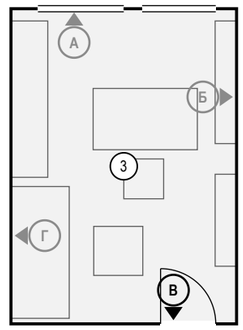

Условные обозначения

- розетка с заземляющим контактом; у знака — марка, ×N постов в рамке, гр. — группа щита, Н — высота оси, мм
- выключатель одноклавишный
- выключатель двухклавишный (флажков — по числу клавиш)
- привязки точек и выводов от угла и от пола, мм
- мебель и приборы — фасад по расстановке (условно)
- зеркало: марка Д, крест — центр, Н — высота центра, мм
- дверь скрытого монтажа: полотно в плоскости стены (узел — на листе узлов)
- стены и перекрытия в сечении
- окраска: тон — цвет по коду производителя (условно)
- О1 — марка отделки по реестру отделки альбома
- А — марка развёртки: буква стены, стрелка — взгляд

Ведомость отделки (на листе)

Марка	Поверхность	Материал, изделие	Цвет, код	Кол.
О1	стены	окраска, Farrow & Ball Modern Emulsion, матовая, подготовка Q3	Farrow & Ball No. 15 «Bone — мягкий каменно-серый с зеленцой»	7,2 м²
О3	плинтус	плинтус МДФ, h 80 мм, аналог: плинтус МДФ под покраску 80×16	Farrow & Ball No. 15 «Bone — мягкий каменно-серый с зеленцой»	2,8 м
О4	потолок	окраска, Tikkurila Anti-Reflex 2, глубокоматовая, подготовка Q3	Tikkurila V503 «Winter»	18,9 м²

Допущения и предложения на листе

Основа листа: размеры сняты с растрового плана заказчика с частичными размерами: рисунок не в масштабе, помещения выровнены по подписанным размерам мебели и проходов; контрольный обмер не выполнен (К-1); высота потолка 2700 мм принята: на плане заказчика её нет (К-2); толщины стен 300 / 120 мм приняты по плану заказчика, не замерены (К-1); разрешённая мощность 15 кВт принята по типовым ТУ для квартиры, ТУ заказчиком не переданы (К-4); подрайон климата не задан — принят не северный (жилые от 2,5 м) (К-6).

См. лист открытых вопросов (лист 6, записи К-1, К-2, К-4, К-6).

Примечания

1. Развёртки — вид на стену изнутри помещения, по часовой стрелке; расположение — на схеме листа и на листе 85; размеры — в мм по чистовым поверхностям; отметки — в м от ±0,000; высоты Н — от чистого пола помещения до оси изделия, у декора — до центра.
2. Красная цепочка — привязки электроточек и выводов по осям от угла чистовых стен; высота Н — у знака, от чистого пола до оси; высоты мебели, проёмов и границ отделки — колонкой отметок слева. Стена с 5 и более точками или с мелкими звеньями привязок показана двумя видами: архитектурная развёртка (мебель, отделка, проёмы, высоты) и вид «Привязки» на отдельном листе — точки и выводы с марками, одна цепочка по осям и таблица привязок (каждая точка — строка).
3. У знака электроточки: марка (Р — розетка, S — выключатель, Св — светильник, ЭВ — вывод кабеля), ×N — число постов в рамке, гр. — группа щита, Н — высота оси от чистого пола, мм; группы по клавишам выключателя — на листе выключателей.
4. Схема мебели, приборов и декора не является технической документацией для производства мебели; габариты — по паспортам изделий.
5. Картины и зеркала крепить к основанию по паспорту изделия (закладные и анкеры — в перечне скрытых работ); крест — ось центра предмета.
6. Двери скрытого монтажа — полотно в плоскости стены, отделка стены по полотну, плинтус прерывается у короба (узел — на листе узлов).
7. Потолок — у каждой стены свой, по плану потолков (ПТ1); ступени — зоной, кромка короба перед нишей — тонкой линией; в поле потолка: ПТ2 +2,600.

1000 мм · печать 1:1

Изм.	Кол.уч	Лист	№ док.	Подп.	Дата
Разраб.		Кырлан А.С.			04.11.26
Пров.					
ГИП					
Н. контр.					
Утв.					

ГД-2026-008-АИ

Квартира с кабинетом

Общая площадь 127,29* м² · * размеры со скана, не замерены (реестр — л. 6–8, К-1)

Дизайн-проект интерьера

Стадия	Лист	Листов
РП	95	131

Развёртка стены В. Кабинет (пом. 3)

М 1:20

Кырлан Александр Сергеевич

выпуск 04.11.2026 № 4177cbe7a3 · стр. 104 из 166

Развёртка стены Г. Кабинет (пом. 3)

Кабинет (пом. 3) · вид изнутри помещения · размеры в мм, отметки в м

ПРЕДВАРИТЕЛЬНО · не для производства работ · открыто пунктов: 13 (реестр — л. 6–8)

Развёртка стены Г


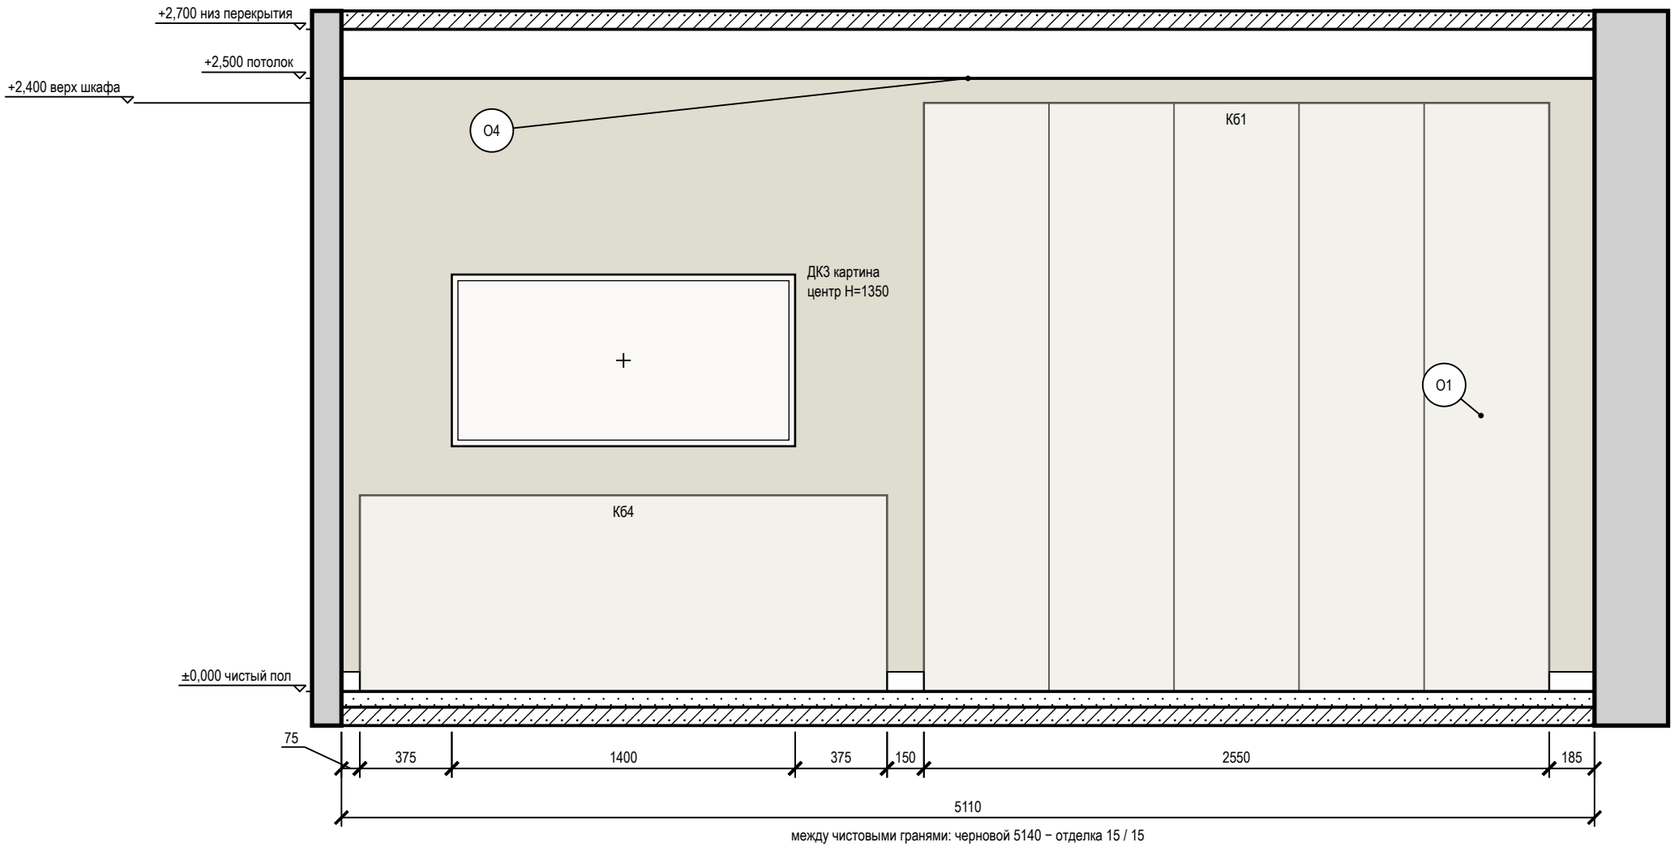


Схема развёрток (М 1:100)

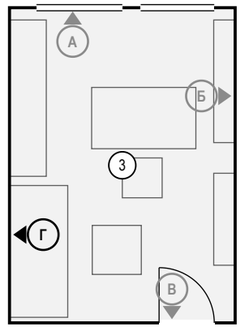

Условные обозначения

- мебель и приборы — фасад по расстановке (условно)
- картина (декор): марка Д, крест — центр, Н — высота центра, мм
- стены и перекрытия в сечении
- окраска: тон — цвет по коду производителя (условно)
- О1 — марка отделки по реестру отделки альбома
- А — марка развёртки: буква стены, стрелка — взгляд

Ведомость отделки (на листе)

Марка	Поверхность	Материал, изделие	Цвет, код	Кол.
О1	стены	окраска, Farrow & Ball Modern Emulsion, матовая, подготовка Q3	Farrow & Ball No. 15 «Bone — мягкий каменно-серый с зеленцой»	12,8 м²
О3	плинтус	плинтус МДФ, h 80 мм, аналог: плинтус МДФ под покраску 80×16	Farrow & Ball No. 15 «Bone — мягкий каменно-серый с зеленцой»	0,4 м
О4	потолок	окраска, Tikkurila Anti-Reflex 2, глубокоматовая, подготовка Q3	Tikkurila V503 «Winter»	18,9 м²

Примечания

1. Развёртки — вид на стену изнутри помещения, по часовой стрелке; расположение — на схеме листа и на листе 85; размеры — в мм по чистовым поверхностям; отметки — в м от ±0,000; высоты Н — от чистого пола помещения до оси изделия, у декора — до центра.
2. Схема мебели, приборов и декора не является технической документацией для производства мебели; габариты — по паспортам изделий.
3. Картины и зеркала крепить к основанию по паспорту изделия (закладные и анкеры — в перечне скрытых работ); крест — ось центра предмета.
4. Потолок — у каждой стены свой, по плану потолков (ПТ1); ступени — зоной, кромка короба перед нишей — тонкой линией; в поле потолка: ПТ2 +2,600.

Допущения и предложения на листе

Основа листа: размеры сняты с растрового плана заказчика с частичными размерами: рисунок не в масштабе, помещения выровнены по подписанным размерам мебели и проходов; контрольный обмер не выполнен (К-1); высота потолка 2700 мм принята: на плане заказчика её нет (К-2); толщины стен 300 / 120 мм приняты по плану заказчика, не замерены (К-1); разрешённая мощность 15 кВт принята по типовым ТУ для квартиры, ТУ заказчиком не переданы (К-4); подрайон климата не задан — принят не северный (жилые от 2,5 м) (К-6). См. лист открытых вопросов (лист 6, записи К-1, К-2, К-4, К-6).

1000 мм · печать 1:1

Изм.	Кол.уч	Лист	№ док.	Подп.	Дата
Разраб.		Кырлан А.С.			04.11.26
Пров.					
ГИП					
Н. контр.					
Утв.					

ГД-2026-008-АИ

Квартира с кабинетом

Общая площадь 127,29* м² · * размеры со скана, не замерены (реестр — л. 6–8, К-1)

Дизайн-проект интерьера

Стадия	Лист	Листов
РП	96	131

Развёртка стены Г. Кабинет (пом. 3)

М 1:25


Кырлан Александр Сергеевич

Развёртка стены Г. Кухня-гостиная (пом. 4), кухонный фронт

Кухня-гостиная (пом. 4) · вид изнутри помещения · размеры в мм, отметки в м

ПРЕДВАРИТЕЛЬНО · не для производства работ · открыто пунктов: 13 (реестр — л. 6–8)

Развёртка стены Г

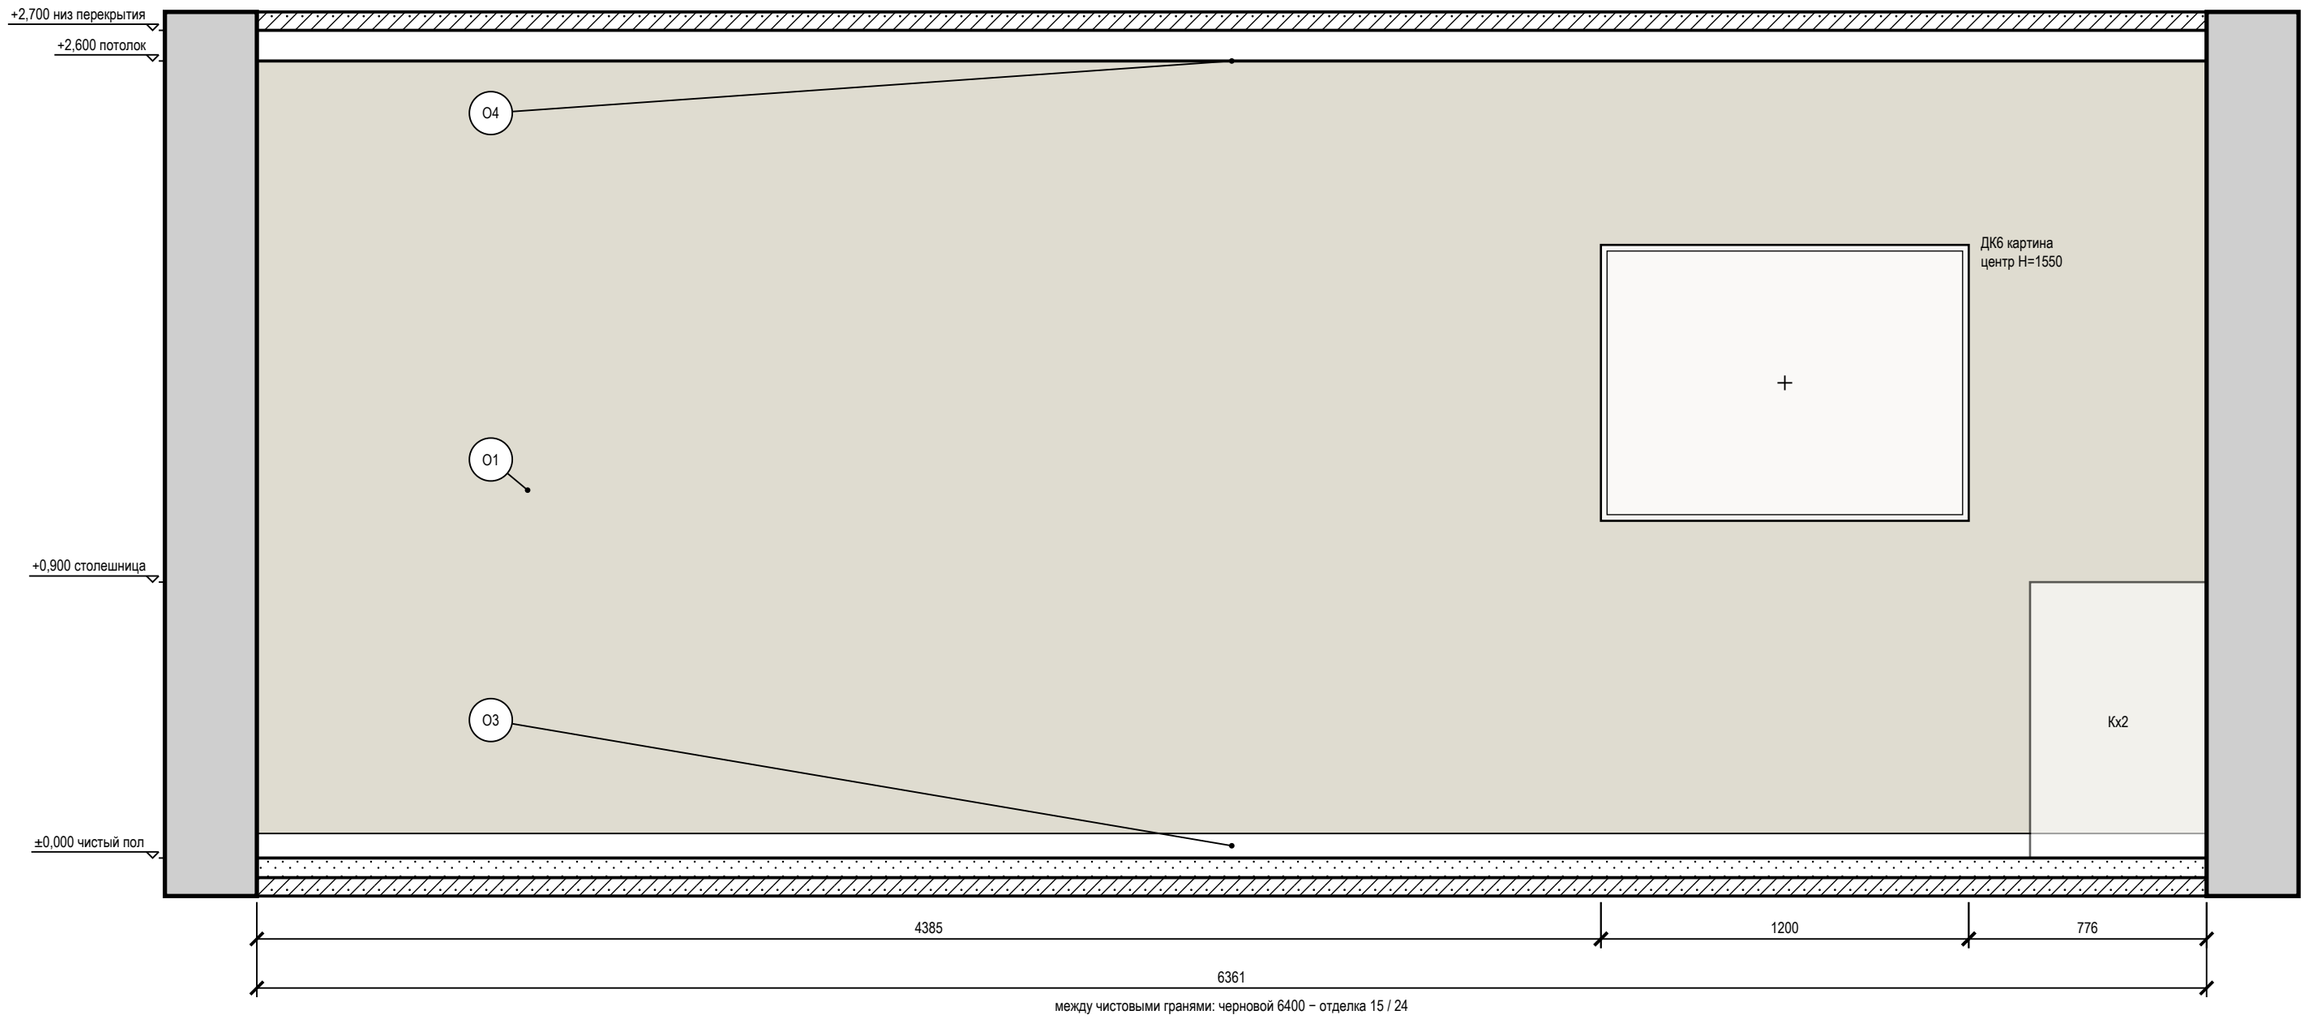

между чистовыми гранями: черновой 6400 − отделка 15 / 24

Условные обозначения

обозначения этого вида, схема развёрток помещения и ведомость отделки — на листе 99

Допущения и предложения на листе

Основа листа: размеры сняты с растрового плана заказчика с частичными размерами: рисунок не в масштабе, помещения выровнены по подписанным размерам мебели и проходов; контрольный обмер не выполнен (К-1); высота потолка 2700 мм принята: на плане заказчика её нет (К-2); толщины стен 300 / 120 мм приняты по плану заказчика, не замерены (К-1); разрешённая мощность 15 кВт принята по типовым ТУ для квартиры, ТУ заказчиком не переданы (К-4); подрайон климата не задан — принят не северный (жилые от 2,5 м) (К-6).
См. лист открытых вопросов (лист 6, записи К-1, К-2, К-4, К-6).

Примечания

1. Развёртки — вид на стену изнутри помещения, по часовой стрелке; расположение — на схеме листа 99 и на листе 85; размеры — в мм по чистовым поверхностям; отметки — в м от ±0,000; высоты Н — от чистого пола помещения до оси изделия, у декора — до центра.
2. Стена Г показана двумя видами: здесь — архитектурная развёртка (мебель, отделка, проёмы, высоты), электроточки и выводы ВК с привязками и таблицей — на листе 98 («Привязки»).
3. Схема мебели, приборов и декора не является технической документацией для производства мебели; габариты — по паспортам изделий.
4. Картины и зеркала крепить к основанию по паспорту изделия (закладные и анкеры — в перечне скрытых работ); крест — ось центра предмета.
5. Потолок — у каждой стены свой, по плану потолков (ПТ2); ступени — зоной, кромка короба перед нишей — тонкой линией; в поле потолка: ПТ1 +2,500.

1000 мм · печать 1:1

Изм.	Кол.уч	Лист	№ док.	Подп.	Дата
Разраб.		Кырлан А.С.			04.11.26
Пров.					
ГИП					
Н. контр.					
Утв.					

ГД-2026-008-АИ

Квартира с кабинетом

Общая площадь 127,29* м² · * размеры со скана, не замерены (реестр — л. 6–8, К-1)

Дизайн-проект интерьера

Стадия	Лист	Листов
РП	97	131

Развёртка стены Г. Кухня-гостиная (пом. 4), кухонный фронт

М 1:20

Кырлан Александр Сергеевич

выпуск 04.11.2026 № 4177cbe7a3 · стр. 106 из 166

Привязки электроточек, стена Г. Кухня-гостиная (пом. 4)

Кухня-гостиная (пом. 4) · вид изнутри помещения · привязки в мм, отметки в м · к развёртке на листе 97

ПРЕДВАРИТЕЛЬНО · не для производства работ · открыто пунктов: 13 (реестр — л. 6–8)

Развёртка стены Г: электроточки и выводы

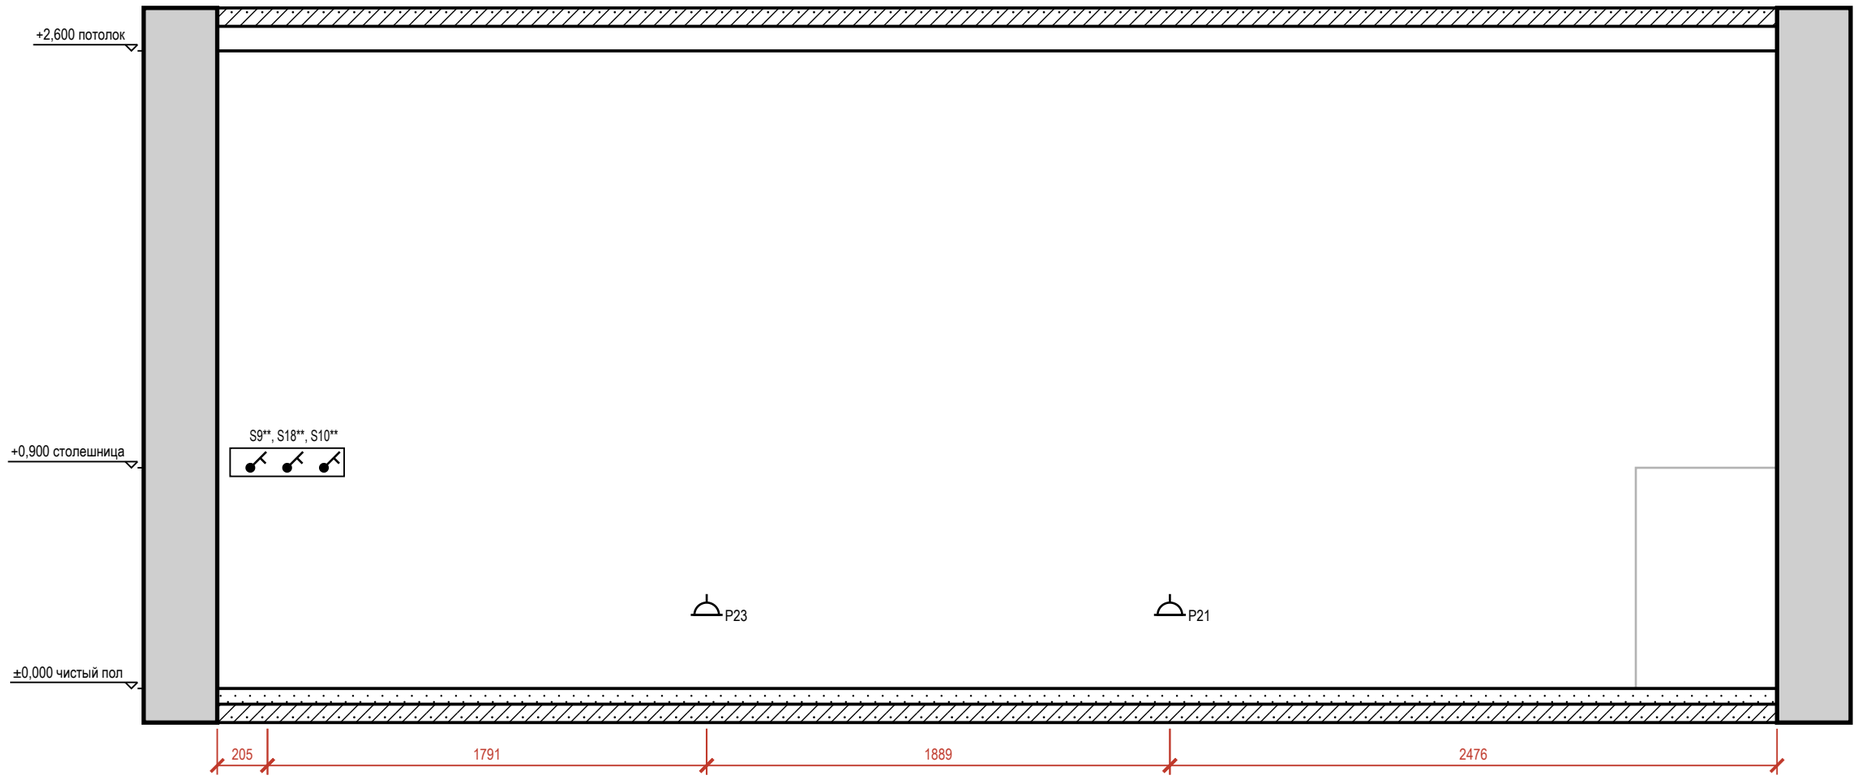


Таблица привязок электроточек и выводов

Марка	Назначение	От угла, мм	H от пола, мм	Примечание
S9**	выключатель	205	900	гр. 2
S18**	выключатель	285	900	гр. 2
S10**	выключатель	365	900	гр. 2
P23	розетка: уборка, пылесос	1996	300	гр. 6
P21	розетка: общего назначения	3885	300	гр. 6

Условные обозначения

- розетка с заземляющим контактом; у знака — марка, ×N постов в рамке, гр. — группа щита, H — высота оси, мм
- выключатель одноклавишный
- привязки точек и выводов от угла и от пола, мм

Примечания

1. Вид «Привязки» стены Г — электроточки и выводы ВК; архитектурная развёртка (мебель, отделка, проёмы, высоты) — на листе 97, расположение — на листе 85. Мебель и приборы — подложкой для ориентира; их марки и обозначения мебели, проёмов и стен — там же.
2. Привязки — в мм: по горизонтали от левого чистового угла стены до оси изделия, H — от чистого пола до оси; все точки — в таблице привязок. Красная цепочка — привязки по осям; точки ближе 150 мм одна к другой в цепочку не дробятся — их привязки только в таблице.
3. У знака — марка электроточки (P — розетка, S — выключатель, Св — светильник, ЭВ — вывод кабеля); посты в рамке и группа щита — в графе «Примечание»; группы по клавишам выключателя — на листе выключателей.
4. Выводы кухонной техники — по утверждённому проекту кухни: привязки выводов даются от осей модулей гарнитура.

Допущения и предложения на листе

Основа листа: размеры сняты с растрового плана заказчика с частичными размерами: рисунок не в масштабе, помещения выровнены по подписанным размерам мебели и проходов; контрольный обмер не выполнен (К-1); высота потолка 2700 мм принята: на плане заказчика её нет (К-2); толщины стен 300 / 120 мм приняты по плану заказчика, не замерены (К-1); разрешённая мощность 15 кВт принята по типовым ТУ для квартиры, ТУ заказчиком не переданы (К-4); подрайон климата не задан — принят не северный (жилые от 2,5 м) (К-6). Знак «**» — предложение проектировщика, заказчиком не утверждено (согласовать с заказчиком): S9, S10 — светорегулятор добавлен разработчиком проекта; S18 — свой пост группе L15: сценарии «Вечер», «Ужин», «Готовка» включают её отдельно от L14 — на одном светорегуляторе не набрать.
См. лист открытых вопросов (лист 6, записи К-1, К-2, К-4, К-6).

1000 мм · печать 1:1

Изм.	Кол.уч	Лист	№ док.	Подп.	Дата
Разраб.		Кырлан А.С.			04.11.26
Пров.					
ГИП					
Н. контр.					
Утв.					

ГД-2026-008-АИ

Квартира с кабинетом

Общая площадь 127,29* м² · * размеры со скана, не замерены (реестр — л. 6–8, К-1)

Дизайн-проект интерьера

Стадия	Лист	Листов
РП	98	131

Привязки электроточек, стена Г. Кухня-гостиная (пом. 4)

М 1:25


Кырлан Александр Сергеевич

выпуск 04.11.2026 № 4177cbe7a3 · стр. 107 из 166

Развёртка стены Г: схема и ведомость отделки. Кухня-гостиная (пом. 4)

ПРЕДВАРИТЕЛЬНО · не для производства работ · открыто пунктов: 13 (реестр — л. 6–8)

Схема развёрток (М 1:50)

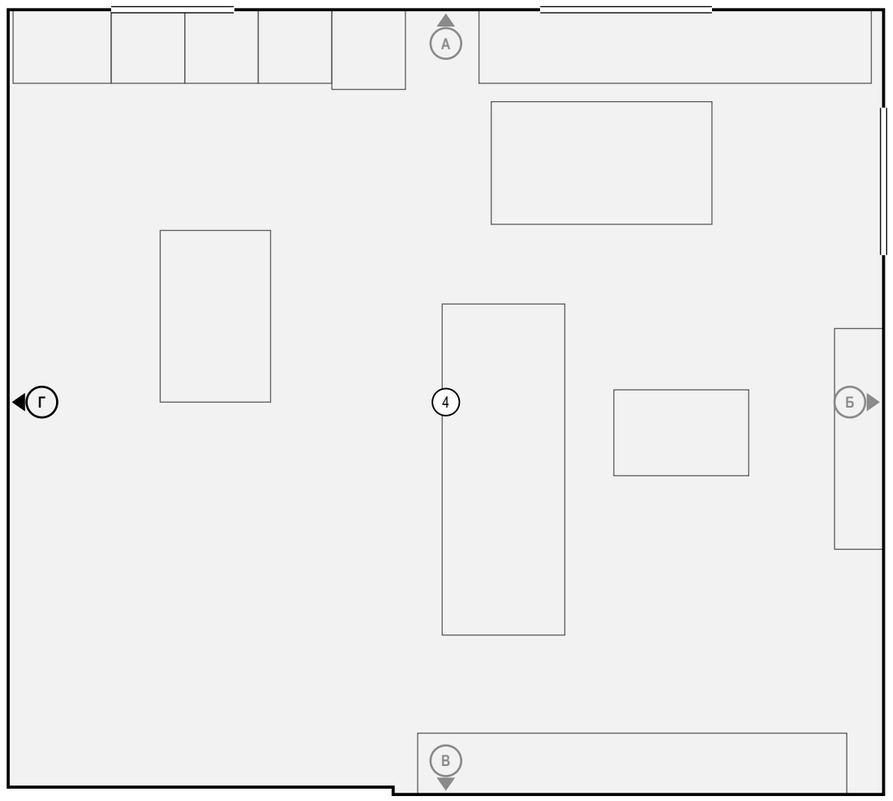

Условные обозначения

- мебель и приборы — фасад по расстановке (условно)
- картина (декор): марка Д, крест — центр, Н — высота центра, мм
- стены и перекрытия в сечении
- окраска: тон — цвет по коду производителя (условно)
- О1 — марка отделки по реестру отделки альбома
- А — марка развёртки: буква стены, стрелка — взгляд

Ведомость отделки (на листе)

Марка	Поверхность	Материал, изделие	Цвет, код	Кол.
О1	стены	окраска, Farrow & Ball Modern Emulsion, матовая, подготовка Q3	Farrow & Ball No. 15 «Bone — мягкий каменно-серый с зеленцой»	16,5 м²
О3	плинтус	плинтус МДФ, h 80 мм, аналог: плинтус МДФ под покраску 80×16	Farrow & Ball No. 15 «Bone — мягкий каменно-серый с зеленцой»	6,4 м
О4	потолок	окраска, Tikkurila Anti-Reflex 2, глубокоматовая, подготовка Q3	Tikkurila V503 «Winter»	45,5 м²

Примечания

1. Схема, условные обозначения и ведомость отделки — к развёртке стены Г на листе 97: вид в своём масштабе занимает лист целиком.
2. Расположение развёрток всех помещений — на листе 85; полная ведомость отделки — на листах отделочника.

Допущения и предложения на листе

Основа листа: размеры сняты с растрового плана заказчика с частичными размерами: рисунок не в масштабе, помещения выровнены по подписанным размерам мебели и проходов; контрольный обмер не выполнен (К-1); высота потолка 2700 мм принята: на плане заказчика её нет (К-2); толщины стен 300 / 120 мм приняты по плану заказчика, не замерены (К-1); разрешённая мощность 15 кВт принята по типовым ТУ для квартиры, ТУ заказчиком не переданы (К-4); подрайон климата не задан — принят не северный (жилые от 2,5 м) (К-6). Знак «**» — предложение проектировщика, заказчиком не утверждено (согласовать с заказчиком): плинтус пом. 4, фартук пом. 4 — артикул изделия не выбран: позиция описана характеристиками («аналог по характеристикам»), артикул выбирается при закупке.

См. лист открытых вопросов (лист 6, записи К-1, К-2, К-4, К-6).

Изм.	Кол.уч	Лист	№ док.	Подп.	Дата
Разраб.		Кырлан А.С.			04.11.26
Пров.					
ГИП					
Н. контр.					
Утв.					

ГД-2026-008-АИ

Квартира с кабинетом

Общая площадь 127,29* м² · * размеры со скана, не замерены (реестр — л. 6–8, К-1)

Дизайн-проект интерьера

Стадия	Лист	Листов
РП	99	131

Развёртка стены Г: схема и ведомость отделки. Кухня-гостиная (пом. 4)

М б/м


Кырлан Александр Сергеевич

Развёртка стены А. Кухня-гостиная (пом. 4), кухонный фронт

Кухня-гостиная (пом. 4) · вид изнутри помещения · размеры в мм, отметки в м

ПРЕДВАРИТЕЛЬНО · не для производства работ · открыто пунктов: 13 (реестр — л. 6–8)

Развёртка стены А

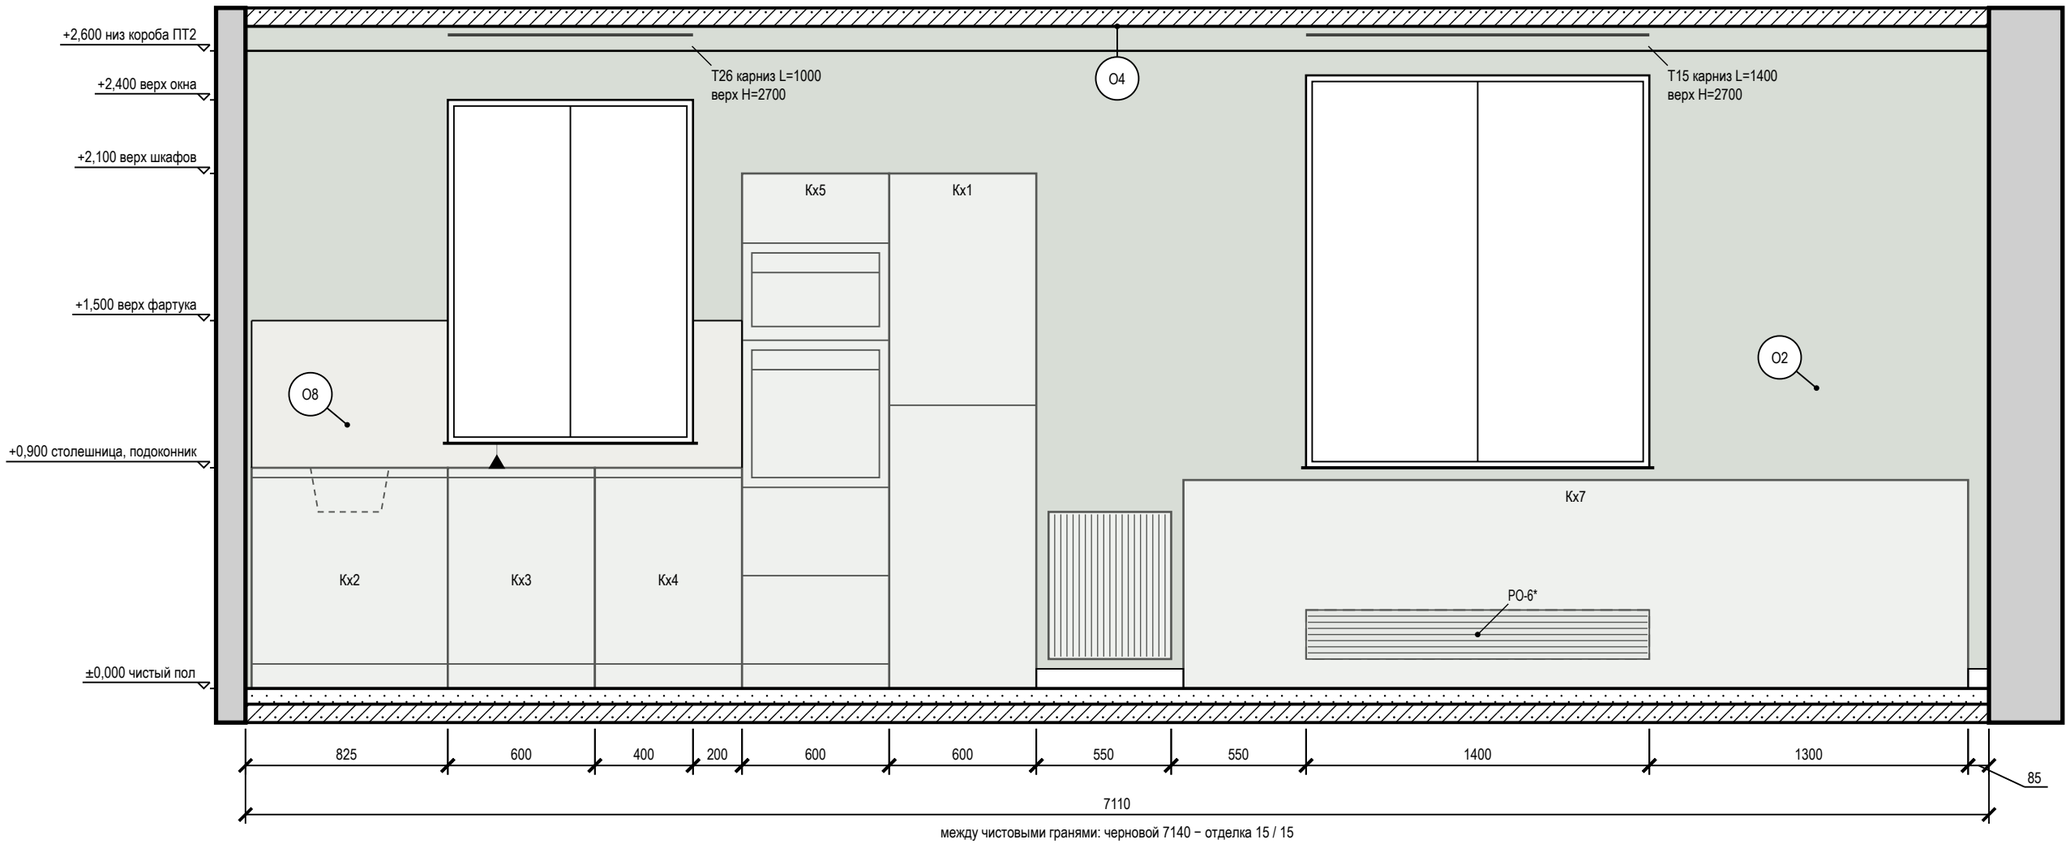

Условные обозначения

обозначения этого вида, схема развёрток помещения и ведомость отделки — на листе 102

Допущения и предложения на листе

Основа листа: размеры сняты с растрового плана заказчика с частичными размерами: рисунок не в масштабе, помещения выровнены по подписанным размерам мебели и проходов; контрольный обмер не выполнен (К-1); высота потолка 2700 мм принята: на плане заказчика её нет (К-2); толщины стен 300 / 120 мм приняты по плану заказчика, не замерены (К-1); разрешённая мощность 15 кВт принята по типовым ТУ для квартиры, ТУ заказчиком не переданы (К-4); подрайон климата не задан — принят не северный (жилые от 2,5 м) (К-6).

Знак «*» — принято, не замерено и не подтверждено (замерить на объекте): ИЗ-7, К-1, К-19: РО-6 — низкий панельный прибор под сиденьем банкетки-экрана Кх7 у окна 2: было 900×600 (верх +720) — под сиденье банкетки не вставал (Кф-2); стало 1400×200, низ +120, верх +320 — по ширине окна, длина компенсирует малую высоту; мощность сверить теплотехническим расчётом ОВ (при нехватке — внутрипольный конвектор у окна).

См. лист открытых вопросов (лист 6, записи К-1, К-2, К-4, К-6; лист 7, запись К-19; лист 8, запись ИЗ-7).

Примечания

1. Развёртки — вид на стену изнутри помещения, по часовой стрелке; расположение — на схеме листа 102 и на листе 85; размеры — в мм по чистовым поверхностям; отметки — в м от ±0,000; высоты Н — от чистого пола помещения до оси изделия, у декора — до центра.
2. Стена А показана двумя видами: здесь — архитектурная развёртка (мебель, отделка, проёмы, высоты), электроточки и выводы ВК с привязками и таблицей — на листе 101 («Привязки»).
3. Схема мебели, приборов и декора не является технической документацией для производства мебели; габариты — по паспортам изделий.
4. Радиатор за корпусом мебели — штриховой линией; горизонтальные ламели — решётка экрана в лицевой панели по ширине прибора, щель для тёплого воздуха над прибором — по чертежу изделия.
5. Карнизы (шины) — по ведомости текстиля декоратора: длина L и верх Н на развёртке — те же числа, что в ведомости; крепление — до окраски потолка.
6. Высота фартука принята 600 мм над столешницей там, где нет навесных модулей и высота фартука не задана.
7. Потолок — у каждой стены свой, по плану потолков (НШ2, ПТ2); ступени — зоной, кромка короба перед нишей — тонкой линией; в поле потолка: ПТ1 +2,500.

1000 мм · печать 1:1

Изм.	Кол.уч	Лист	№ док.	Подп.	Дата
Разраб.		Кырлан А.С.			04.11.26
Пров.					
ГИП					
Н. контр.					
Утв.					

ГД-2026-008-АИ

Квартира с кабинетом

Общая площадь 127,29* м² · * размеры со скана, не замерены (реестр — л. 6–8, К-1)

Дизайн-проект интерьера	Стадия	Лист	Листов
	РП	100	131

Развёртка стены А. Кухня-гостиная (пом. 4), кухонный фронт

М 1:25

Кырлан Александр Сергеевич

выпуск 04.11.2026 № 4177cbe7a3 · стр. 109 из 166

Привязки электроточек и выводов ВК, стена А. Кухня-гостиная (пом. 4)

Кухня-гостиная (пом. 4) · вид изнутри помещения · привязки в мм, отметки в м · к развёртке на листе 100

ПРЕДВАРИТЕЛЬНО · не для производства работ · открыто пунктов: 13 (реестр — л. 6–8)

Развёртка стены А: электроточки и выводы

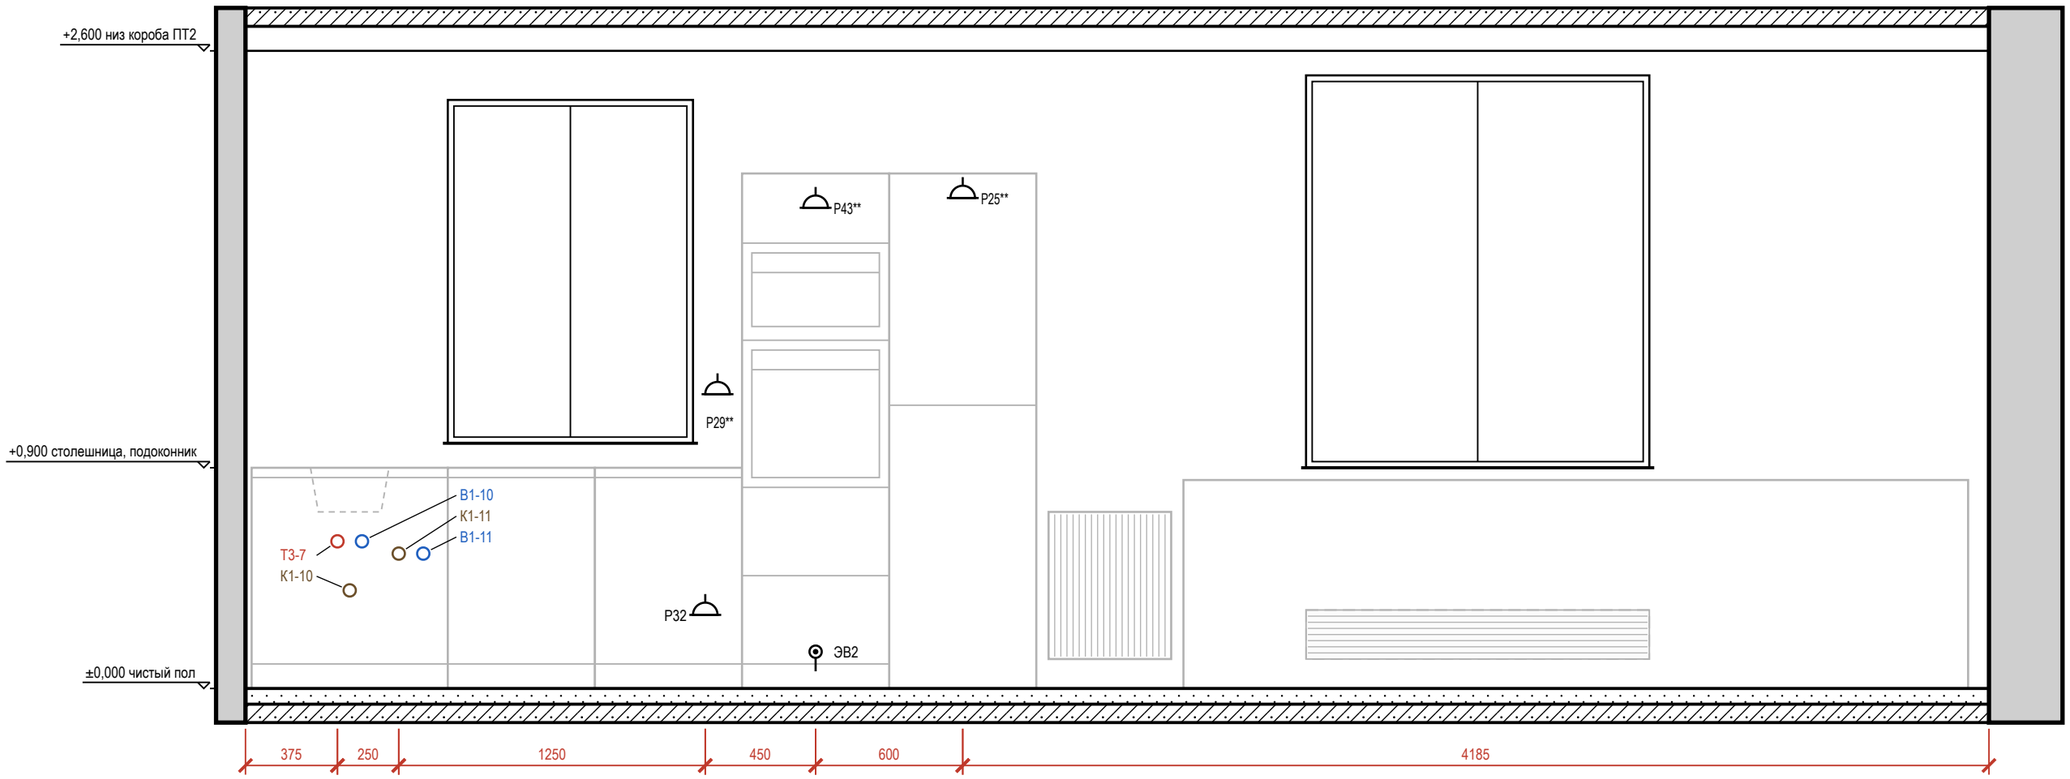


Таблица привязок электроточек и выводов

Марка	Назначение	От угла, мм	Н от пола, мм	Примечание
Т3-7	горячая вода — мойка кухонная	375	600*	межос. 100
К1-10	канализация — мойка кухонная	425	400*	Ø50
В1-10	холодная вода — мойка кухонная	475	600*	межос. 100
К1-11	канализация — посудомоечная машина	625	550*	Ø40; слив ПММ в шкафу мойки
В1-11	холодная вода — посудомоечная машина	725	550*	кран ПММ в шкафу мойки

Марка	Назначение	От угла, мм	Н от пола, мм	Примечание
P32	розетка: посудомоечная машина — в соседнем модуле, за ящиком	1875	300	гр. 10
P29**	розетка: фартук	1925	1200	гр. 7
ЭВ2	вывод кабеля: духовой шкаф — в цоколе	2325	150	гр. 9
P43**	розетка: СВЧ — над нишей, съёмная панель	2325	1960	гр. 7
P25**	розетка: холодильник — над нишей, съёмная панель	2925	2000	гр. 11

Условные обозначения

- розетка с заземляющим контактом; у знака — марка, ×N — постов в рамке, гр. — группа щита, Н — высота оси, мм
- вывод кабеля для подключения прибора (без розетки), марка ЭВ
- вывод В1 (код — в ведомости привязок)
- вывод Т3 (код — в ведомости привязок)
- вывод К1 (код — в ведомости привязок)
- привязки точек и выводов от угла и от пола, мм

Примечания

1. Вид «Привязки» стены А — электроточки и выводы ВК; архитектурная развёртка (мебель, отделка, проёмы, высоты) — на листе 100, расположение — на листе 85. Мебель и приборы — подложкой для ориентира; их марки и обозначения мебели, проёмов и стен — там же.
2. Привязки — в мм: по горизонтали от левого чистового угла стены до оси изделия, Н — от чистого пола до оси; все точки — в таблице привязок. Красная цепочка — привязки по осям; точки ближе 150 мм одна к другой в цепочку не дробятся — их привязки только в таблице.
3. У знака — марка электроточки (Р — розетка, S — выключатель, Св — светильник, ЭВ — вывод кабеля); посты в рамке и группа щита — в графе «Примечание»; группы по клавишам выключателя — на листе выключателей.
4. Коды выводов ВК: В1 — холодная вода, Т3 — горячая вода, К1 — канализация; номер после дефиса — номер вывода на листе выводов сантехники; * — высота принята по типовой практике монтажа, окончательно — по паспорту прибора.
5. Выводы кухонной техники — по утверждённому проекту кухни: привязки выводов даются от осей модулей гарнитура.

Допущения и предложения на листе. Основа листа: размеры сняты с растрового плана заказчика с частичными размерами: рисунок не в масштабе, помещения выровнены по подписанным размерам мебели и проходов; контрольный обмер не выполнен (К-1); высота потолка 2700 мм принята: на плане заказчика её нет (К-2); толщины стен 300 / 120 мм приняты по плану заказчика, не замерены (К-1); разрешённая мощность 15 кВт принята по типовым ТУ для квартиры, ТУ заказчиком не переданы (К-4); подрайон климата не задан — принят не северный (жилые от 2,5 м) (К-6). Знак «**» — предложение проектировщика, заказчиком не утверждено (согласовать с заказчиком): P25 — высота 2000 мм выше нормы 1 м (ПУЭ 6.6.30) по назначению: розетка встроенного прибора — в колонне Кх1 над нишей, в антресоли за съёмной панелью; P29 — Сдвиг под раскладку плитки фартука (стена А) на 100 мм выше — ось на шве или в центре плитки, привязка по таблице листа; P43 — высота 1960 мм выше нормы 1 м (ПУЭ 6.6.30) по назначению: розетка встроенного прибора — в колонне Кх5 над нишей, в антресоли за съёмной панелью. См. лист открытых вопросов (лист 6, записи К-1, К-2, К-4, К-6).

1000 мм · печать 1:1

Изм.	Кол.уч	Лист	№ док.	Подп.	Дата
Разраб.		Кырлан А.С.			04.11.26
Пров.					
ГИП					
Н. контр.					
Утв.					

ГД-2026-008-АИ

Квартира с кабинетом

Общая площадь 127,29* м² · * размеры со скана, не замерены (реестр — л. 6–8, К-1)

Дизайн-проект интерьера

Стадия	Лист	Листов
РП	101	131

Привязки электроточек и выводов ВК, стена А. Кухня-гостиная (пом. 4)

М 1:25

Кырлан Александр Сергеевич


выпуск 04.11.2026 № 4177cbe7a3 · стр. 110 из 166

Развёртка стены А: схема и ведомость отделки. Кухня-гостиная (пом. 4)

Кухня-гостиная (пом. 4) · к развёртке на листе 100

ПРЕДВАРИТЕЛЬНО · не для производства работ · открыто пунктов: 13 (реестр — л. 6–8)

Схема развёрток (М 1:50)

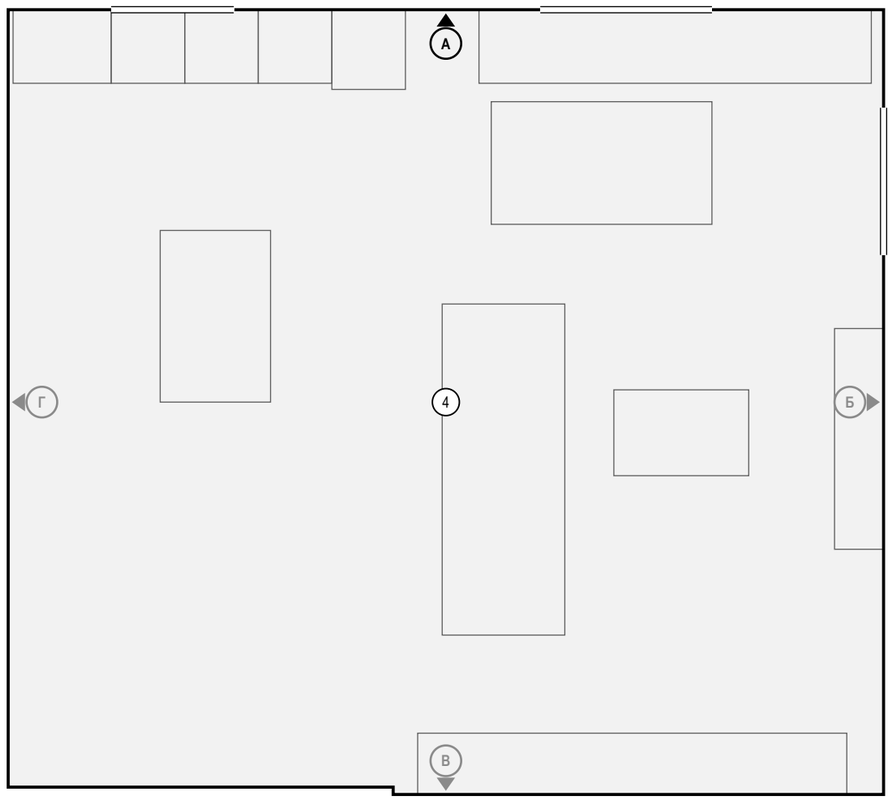

Условные обозначения

- мебель и приборы — фасад по расстановке (условно)
- карниз (шина) и шторы в собранном виде: марка Т, длина L, верх Н
- окно: проём, рама, подоконник
- радиатор отопления; марка — по плану отопления
- стены и перекрытия в сечении
- плитка: сетка швов по формату, ▲ — ось старта
- окраска: тон — цвет по коду производителя (условно)
- О1 — марка отделки по реестру отделки альбома
- А — марка развёртки: буква стены, стрелка — взгляд

Ведомость отделки (на листе)

Марка	Поверхность	Материал, изделие	Цвет, код	Кол.
О2	акцентная стена	окраска, Farrow & Ball Modern Emulsion, матовая, подготовка Q3	Farrow & Ball No. 34 «Calke Green традиционный шалфей»	14,4 м²
О3	плинтус	плинтус МДФ, h 80 мм, аналог: плинтус МДФ под покраску 80×16	Farrow & Ball No. 15 «Bone — мягкий каменно-серый с зеленцой»	0,7 м
О4	потолок	окраска, Tikkurila Anti-Reflex 2, глубокоматовая, подготовка Q3	Tikkurila V503 «Winter»	45,5 м²
О8	фартук	керамогранит, 1200×600×9 мм, аналог: керамогранит под травертин, матовый, затирка CG2WA		0,7 м²

Примечания

1. Схема, условные обозначения и ведомость отделки — к развёртке стены А на листе 100: вид в своём масштабе занимает лист целиком.
2. Расположение развёрток всех помещений — на листе 85; полная ведомость отделки — на листах отделочника.

Допущения и предложения на листе

Основа листа: размеры сняты с растрового плана заказчика с частичными размерами: рисунок не в масштабе, помещения выровнены по подписанным размерам мебели и проходов; контрольный обмер не выполнен (К-1); высота потолка 2700 мм принята: на плане заказчика её нет (К-2); толщины стен 300 / 120 мм приняты по плану заказчика, не замерены (К-1); разрешённая мощность 15 кВт принята по типовым ТУ для квартиры, ТУ заказчиком не переданы (К-4); подрайон климата не задан — принят не северный (жилые от 2,5 м) (К-6). Знак «**» — предложение проектировщика, заказчиком не утверждено (согласовать с заказчиком): плинтус пом. 4, фартук пом. 4 — артикул изделия не выбран: позиция описана характеристиками («аналог по характеристикам»), артикул выбирается при закупке.

См. лист открытых вопросов (лист 6, записи К-1, К-2, К-4, К-6).

Изм.	Кол.уч	Лист	№ док.	Подп.	Дата
Разраб.		Кырлан А.С.			04.11.26
Пров.					
ГИП					
Н. контр.					
Утв.					

ГД-2026-008-АИ

Квартира с кабинетом

Общая площадь 127,29* м² · * размеры со скана, не замерены (реестр — л. 6–8, К-1)

Дизайн-проект интерьера

Стадия	Лист	Листов
РП	102	131

Развёртка стены А: схема и ведомость отделки. Кухня-гостиная (пом. 4)

М б/м

Кырлан Александр Сергеевич


выпуск 04.11.2026 № 4177cbe7a3 · стр. 111 из 166

Развёртка стены Б. Кухня-гостиная (пом. 4)

Кухня-гостиная (пом. 4) · вид изнутри помещения · размеры в мм, отметки в м

ПРЕДВАРИТЕЛЬНО · не для производства работ · открыто пунктов: 13 (реестр — л. 6–8)

Развёртка стены Б

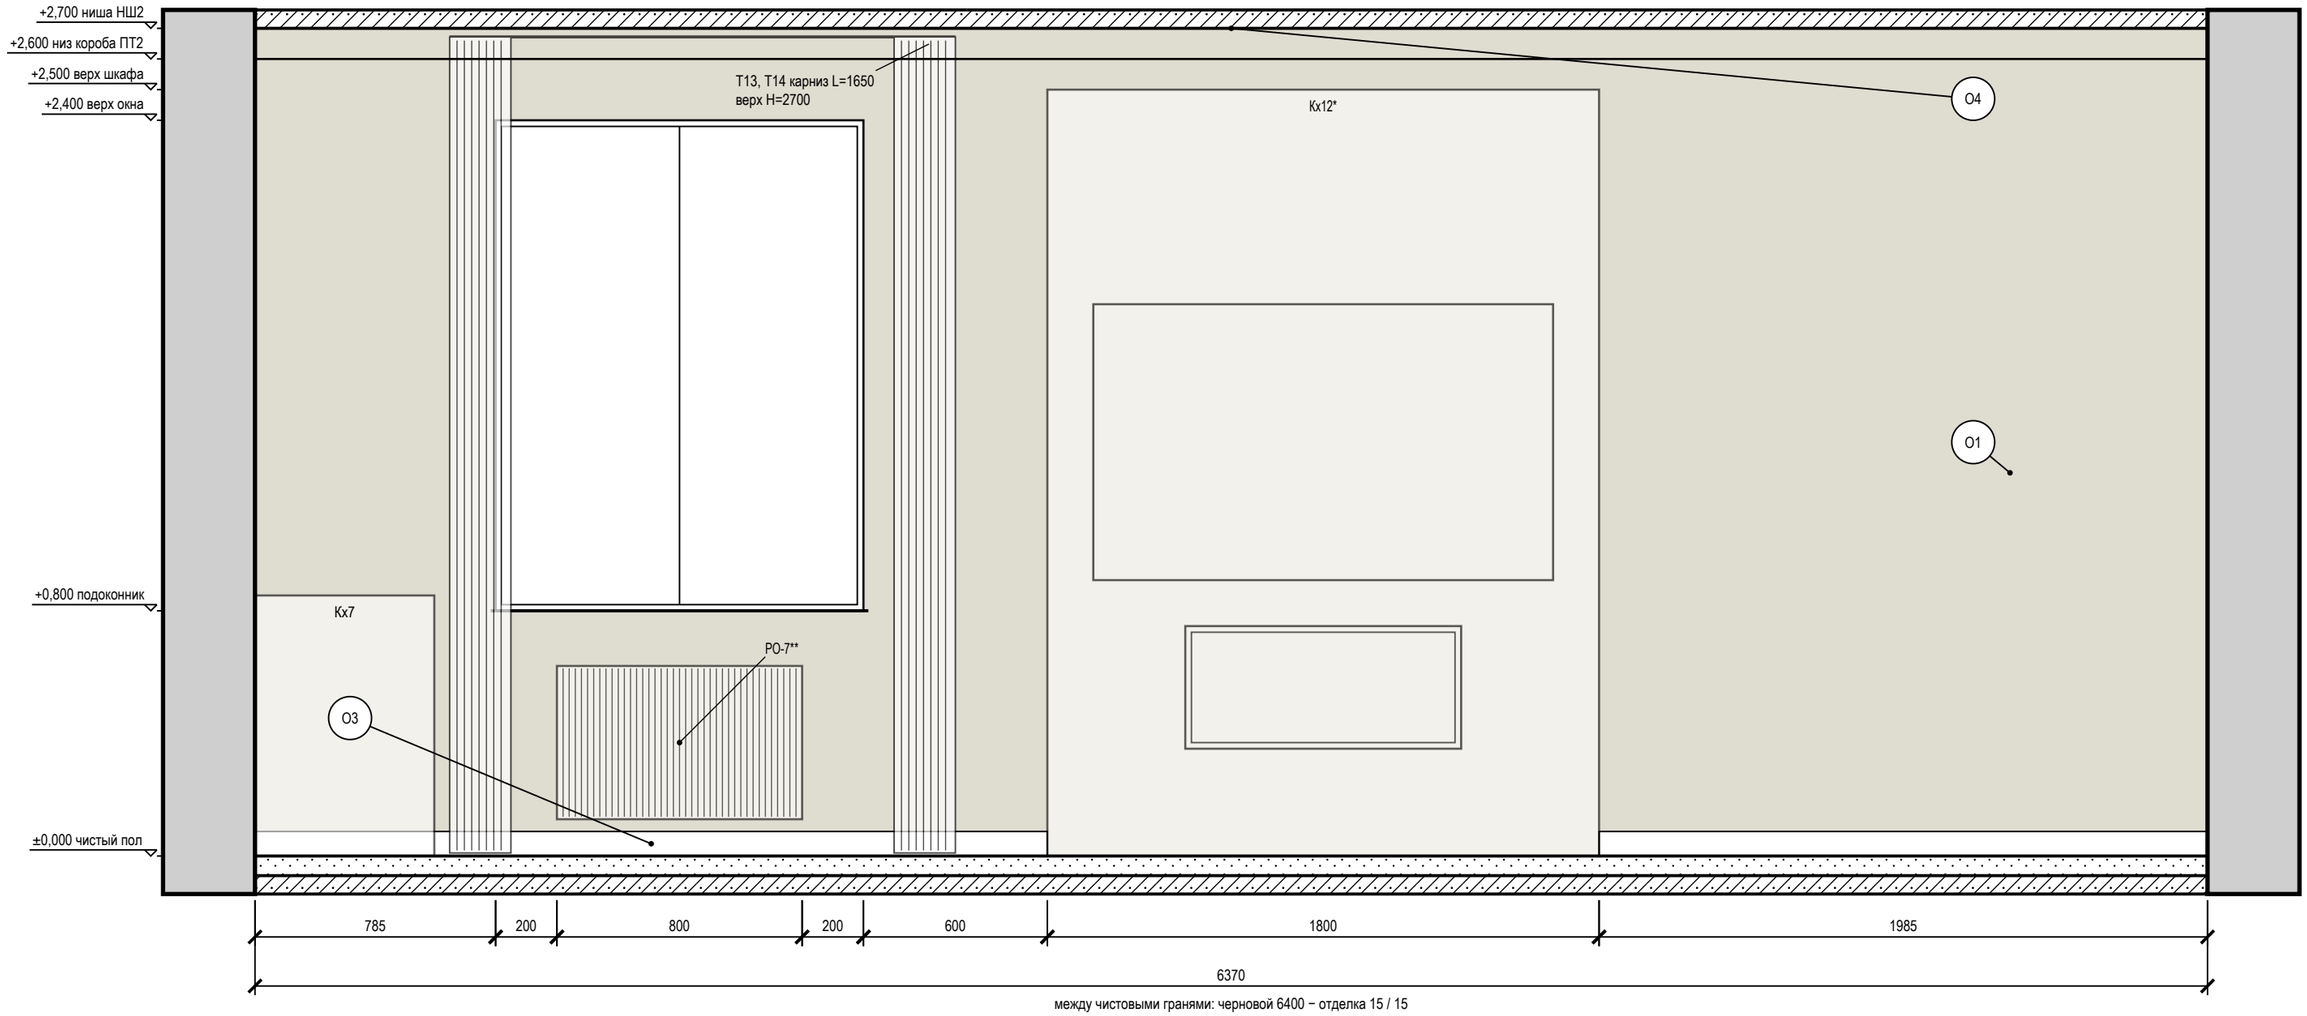

между чистовыми гранями: черновой 6400 − отделка 15 / 15

Условные обозначения

обозначения этого вида, схема развёрток помещения и ведомость отделки — на листе 105

Допущения и предложения на листе. Основа листа: размеры сняты с растрового плана заказчика с частичными размерами: рисунок не в масштабе, помещения выровнены по подписанным размерам мебели и проходов; контрольный обмер не выполнен (К-1); высота потолка 2700 мм принята: на плане заказчика её нет (К-2); толщины стен 300 / 120 мм приняты по плану заказчика, не замерены (К-1); разрешённая мощность 15 кВт принята по типовым ТУ для квартиры, ТУ заказчиком не переданы (К-4); подрайон климата не задан — принят не северный (жилые от 2,5 м) (К-6). Знак «*» — принято, не замерено и не подтверждено (замерить на объекте): ИЗ-5, ИЗ-9, К-20: Кх12 — Было: предмет 1800×400 h 500 на отметке 0 — на развёртке стены Б низкий короб у пола. Знак «**» — предложение проектировщика, заказчиком не утверждено (согласовать с заказчиком): К-1: РО-7 — прибор под окном по оси проёма, ширина ≈ 0,7 ширины окна — предложение ОВ (лист ОВ выводил его сам до, теперь он в данных — один источник для листа, мебели, DXF и IFC); стояки и подводки отопления не замерены, мощность — по теплотехническому расчёту ОВ. См. лист открытых вопросов (лист 6, записи К-1, К-2, К-4, К-6; лист 7, запись К-20; лист 8, записи ИЗ-5, ИЗ-9); по листу — К-20.

Примечания

1. Развёртки — вид на стену изнутри помещения, по часовой стрелке; расположение — на схеме листа 105 и на листе 85; размеры — в мм по чистовым поверхностям; отметки — в м от ±0,000; высоты Н — от чистого пола помещения до оси изделия, у декора — до центра.
2. Стена Б показана двумя видами: здесь — архитектурная развёртка (мебель, отделка, проёмы, высоты), электроточки и выводы ВК с привязками и таблицей — на листе 104 («Привязки»).
3. Схема мебели, приборов и декора не является технической документацией для производства мебели; габариты — по паспортам изделий.
4. Карнизы (шины) — по ведомости текстиля декоратора: длина L и верх Н на развёртке — те же числа, что в ведомости; крепление — до окраски потолка.
5. Потолок — у каждой стены свой, по плану потолков (НШ2, ПТ2); ступени — зоной, кромка короба перед нишей — тонкой линией; в поле потолка: ПТ1 +2,500.

1000 мм · печать 1:1

Изм.	Кол.уч	Лист	№ док.	Подп.	Дата
Разраб.		Кырлан А.С.			04.11.26
Пров.					
ГИП					
Н. контр.					
Утв.					

ГД-2026-008-АИ

Квартира с кабинетом

Общая площадь 127,29* м² · * размеры со скана, не замерены (реестр — л. 6–8, К-1)

Дизайн-проект интерьера

Стадия	Лист	Листов
РП	103	131

Развёртка стены Б. Кухня-гостиная (пом. 4)

М 1:20

Кырлан Александр Сергеевич

выпуск 04.11.2026 № 4177cbe7a3 · стр. 112 из 166

Привязки электроточек, стена Б. Кухня-гостиная (пом. 4)

Кухня-гостиная (пом. 4) · вид изнутри помещения · привязки в мм, отметки в м · к развёртке на листе 103

ПРЕДВАРИТЕЛЬНО · не для производства работ · открыто пунктов: 13 (реестр — л. 6–8)

Развёртка стены Б: электроточки и выводы

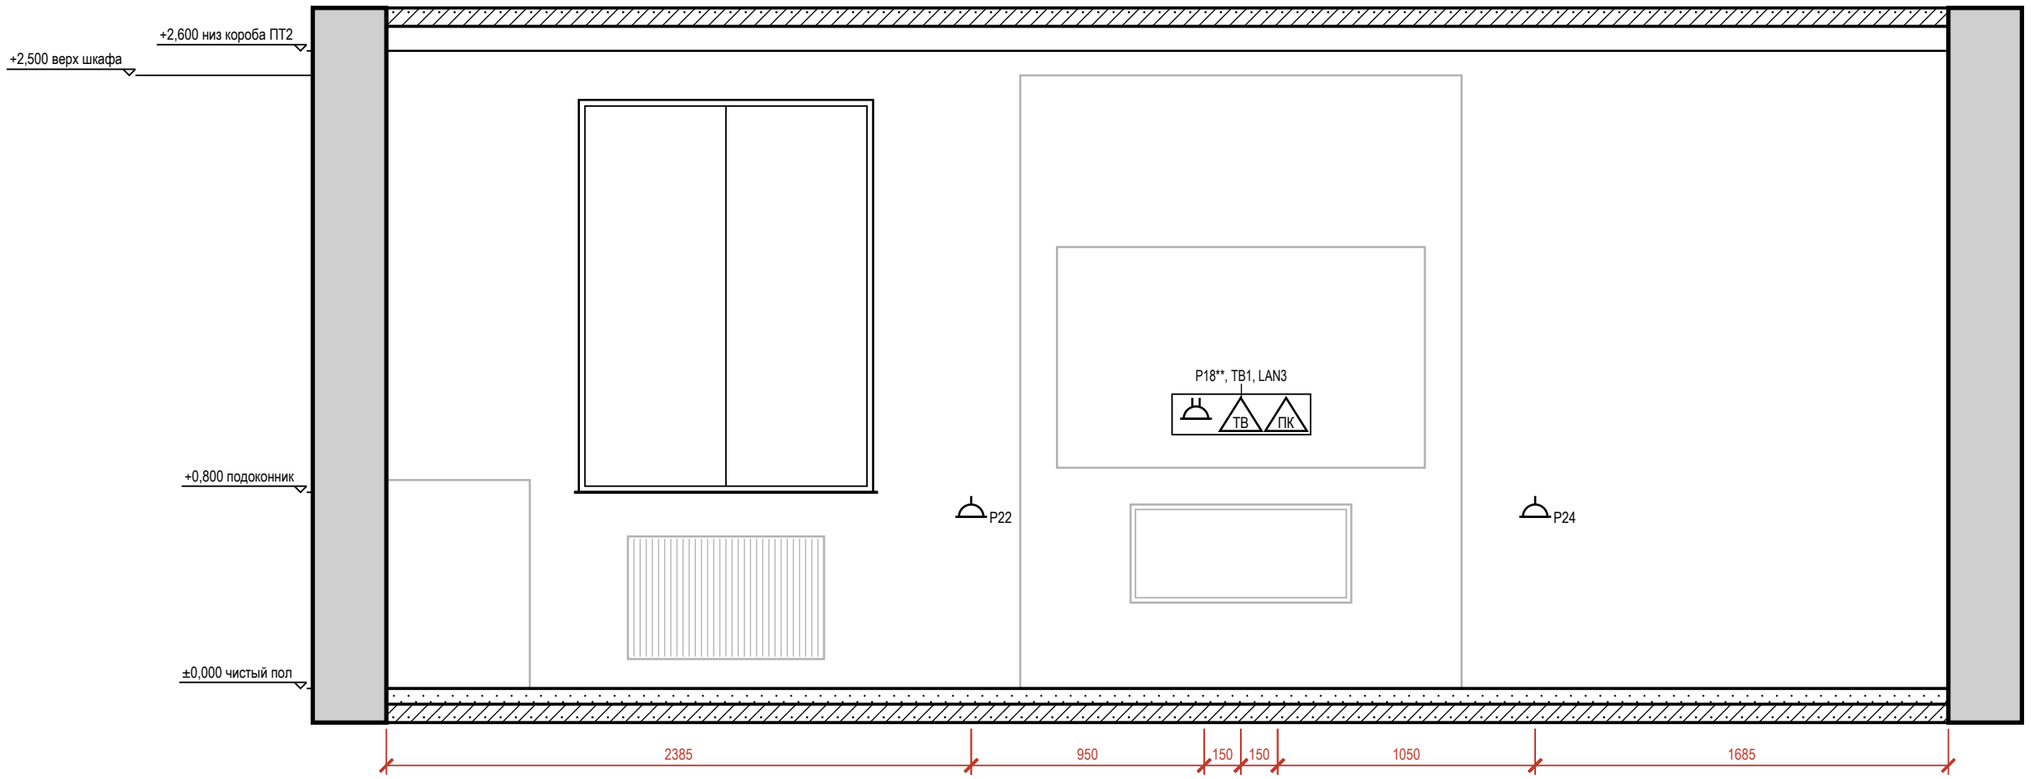


Таблица привязок электроточек и выводов

Марка	Назначение	От угла, мм	Н от пола, мм	Примечание
P22	розетка: общего назначения	2385	700	гр. 6
P18**	розетка: ТВ-зона: питание ТВ и приставки	3335	1100	рамка 2 поста, гр. 6
TB1	розетка ТВ: ТВ-зона	3485	1100	
LAN3	розетка RJ45: ТВ-зона: Smart TV	3635	1100	
P24	розетка: общего назначения	4685	700	гр. 6

Условные обозначения

- розетка с заземляющим контактом; у знака — марка, ×N постов в рамке, гр. — группа щита, Н — высота оси, мм
- ПК — розетка компьютерная RJ45
- ТВ — розетка телевизионная
- привязки точек и выводов от угла и от пола, мм

Примечания

1. Вид «Привязки» стены Б — электроточки и выводы ВК; архитектурная развёртка (мебель, отделка, проёмы, высоты) — на листе 103, расположение — на листе 85. Мебель и приборы — подложкой для ориентира; их марки и обозначения мебели, проёмов и стен — там же.
2. Привязки — в мм: по горизонтали от левого чистового угла стены до оси изделия, Н — от чистого пола до оси; все точки — в таблице привязок. Красная цепочка — привязки по осям; точки ближе 150 мм одна к другой в цепочку не дробятся — их привязки только в таблице.
3. У знака — марка электроточки (Р — розетка, S — выключатель, Св — светильник, ЭВ — вывод кабеля); посты в рамке и группа щита — в графе «Примечание»; группы по клавишам выключателя — на листе выключателей.

Допущения и предложения на листе

Основа листа: размеры сняты с растрового плана заказчика с частичными размерами: рисунок не в масштабе, помещения выровнены по подписанным размерам мебели и проходов; контрольный обмер не выполнен (К-1); высота потолка 2700 мм принята: на плане заказчика её нет (К-2); толщины стен 300 / 120 мм приняты по плану заказчика, не замерены (К-1); разрешённая мощность 15 кВт принята по типовым ТУ для квартиры, ТУ заказчиком не переданы (К-4); подрайон климата не задан — принят не северный (жилые от 2,5 м) (К-6). Знак «**» — предложение проектировщика, заказчиком не утверждено (согласовать с заказчиком): Р18 — Точка в нише ТВ встроенной ТВ-стены Кх12 (ниша 1500×900, низ +900): выведена в корпус изделия, не за ним.

См. лист открытых вопросов (лист 6, записи К-1, К-2, К-4, К-6).

1000 мм · печать 1:1

Изм.	Кол.уч	Лист	№ док.	Подп.	Дата
Разраб.		Кырлан А.С.			04.11.26
Пров.					
ГИП					
Н. контр.					
Утв.					

ГД-2026-008-АИ

Квартира с кабинетом

Общая площадь 127,29* м² · * размеры со скана, не замерены (реестр — л. 6–8, К-1)

Дизайн-проект интерьера

Стадия	Лист	Листов
РП	104	131

Привязки электроточек, стена Б. Кухня-гостиная (пом. 4)

М 1:25


Кырлан Александр Сергеевич

выпуск 04.11.2026 № 4177cbe7a3 · стр. 113 из 166

Развёртка стены Б: схема и ведомость отделки. Кухня-гостиная (пом. 4)

Кухня-гостиная (пом. 4) · к развёртке на листе 103

Схема развёрток (М 1:50)

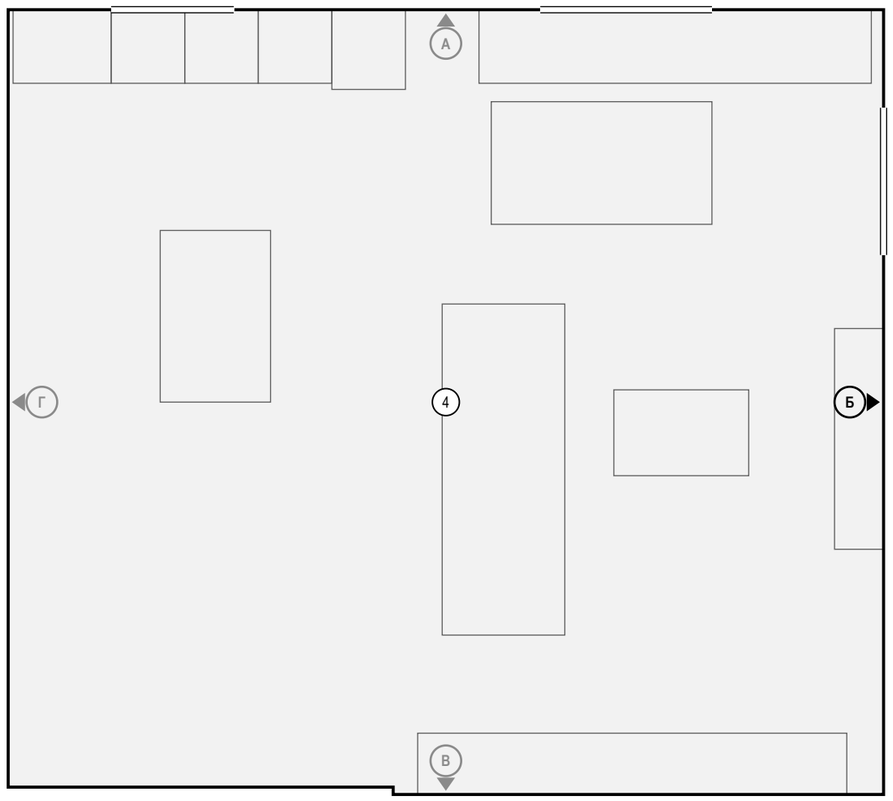

Условные обозначения

- мебель и приборы — фасад по расстановке (условно)
- карниз (шина) и шторы в собранном виде: марка Т, длина L, верх Н
- окно: проём, рама, подоконник
- радиатор отопления; марка — по плану отопления
- стены и перекрытия в сечении
- окраска: тон — цвет по коду производителя (условно)
- О1 — марка отделки по реестру отделки альбома
- А — марка развёртки: буква стены, стрелка — взгляд

Ведомость отделки (на листе)

Марка	Поверхность	Материал, изделие	Цвет, код	Кол.
О1	стены	окраска, Farrow & Ball Modern Emulsion, матовая, подготовка Q3	Farrow & Ball No. 15 «Bone — мягкий каменно-серый с зеленцой»	15,3 м²
О3	плинтус	плинтус МДФ, h 80 мм, аналог: плинтус МДФ под покраску 80×16	Farrow & Ball No. 15 «Bone — мягкий каменно-серый с зеленцой»	4,6 м
О4	потолок	окраска, Tikkurila Anti-Reflex 2, глубокоматовая, подготовка Q3	Tikkurila V503 «Winter»	45,5 м²

Примечания

1. Схема, условные обозначения и ведомость отделки — к развёртке стены Б на листе 103: вид в своём масштабе занимает лист целиком.
2. Расположение развёрток всех помещений — на листе 85; полная ведомость отделки — на листах отделочника.

Допущения и предложения на листе

Основа листа: размеры сняты с растрового плана заказчика с частичными размерами: рисунок не в масштабе, помещения выровнены по подписанным размерам мебели и проходов; контрольный обмер не выполнен (К-1); высота потолка 2700 мм принята: на плане заказчика её нет (К-2); толщины стен 300 / 120 мм приняты по плану заказчика, не замерены (К-1); разрешённая мощность 15 кВт принята по типовым ТУ для квартиры, ТУ заказчиком не переданы (К-4); подрайон климата не задан — принят не северный (жилые от 2,5 м) (К-6). Знак «**» — предложение проектировщика, заказчиком не утверждено (согласовать с заказчиком): плинтус пом. 4, фартук пом. 4 — артикул изделия не выбран: позиция описана характеристиками («аналог по характеристикам»), артикул выбирается при закупке.

См. лист открытых вопросов (лист 6, записи К-1, К-2, К-4, К-6).

Изм.	Кол.уч	Лист	№ док.	Подп.	Дата
Разраб.		Кырлан А.С.			04.11.26
Пров.					
ГИП					
Н. контр.					
Утв.					

ГД-2026-008-АИ

Квартира с кабинетом

Общая площадь 127,29* м² · * размеры со скана, не замерены (реестр — л. 6–8, К-1)

Дизайн-проект интерьера

Стадия	Лист	Листов
РП	105	131

Развёртка стены Б: схема и ведомость отделки. Кухня-гостиная (пом. 4)

М б/м

Кырлан Александр Сергеевич


выпуск 04.11.2026 № 4177cbe7a3 · стр. 114 из 166

Развёртка стены В. Кухня-гостиная (пом. 4)

Кухня-гостиная (пом. 4) · вид изнутри помещения · размеры в мм, отметки в м

ПРЕДВАРИТЕЛЬНО · не для производства работ · открыто пунктов: 13 (реестр — л. 6–8)

Развёртка стены В

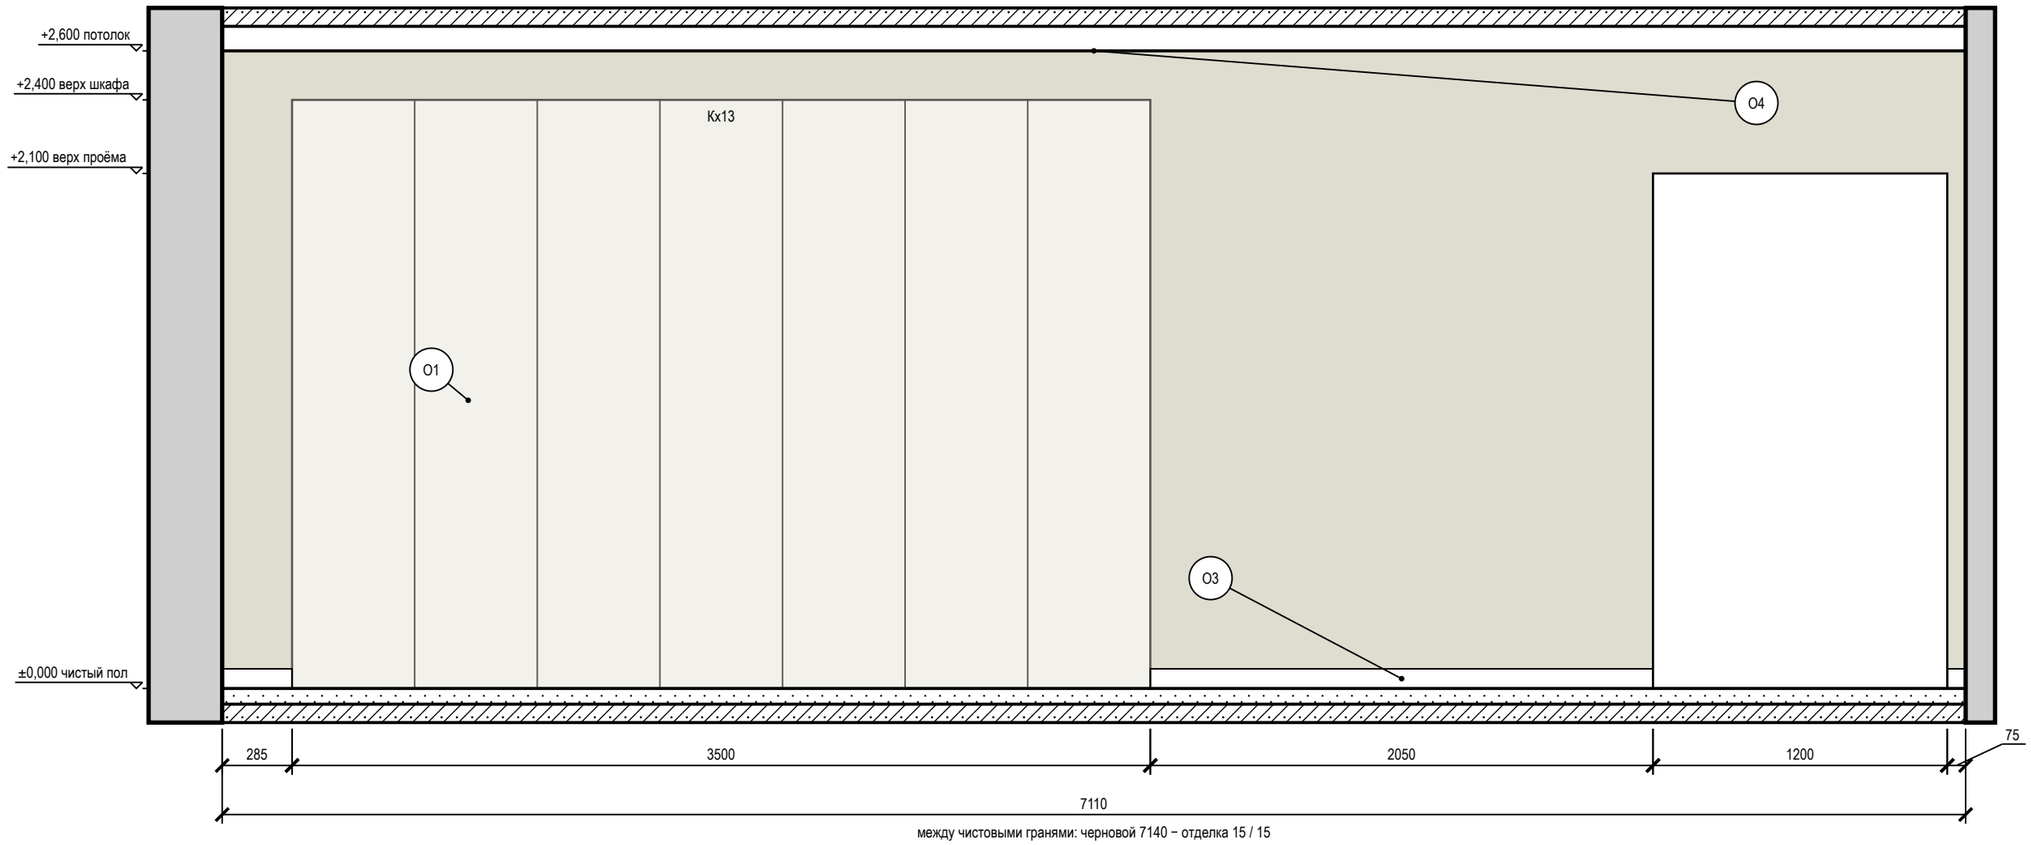

между чистовыми гранями: черновой 7140 − отделка 15 / 15

Условные обозначения

обозначения этого вида, схема развёрток помещения и ведомость отделки — на листе 107

Примечания

1. Развёртки — вид на стену изнутри помещения, по часовой стрелке; расположение — на схеме листа 107 и на листе 85; размеры — в мм по чистовым поверхностям; отметки — в м от ±0,000; высоты Н — от чистого пола помещения до оси изделия, у декора — до центра.
2. Схема мебели, приборов и декора не является технической документацией для производства мебели; габариты — по паспортам изделий.
3. Потолок — у каждой стены свой, по плану потолков (ПТ2); ступени — зоной, кромка короба перед нишей — тонкой линией; в поле потолка: ПТ1 +2,500.

Допущения и предложения на листе

Основа листа: размеры сняты с растрового плана заказчика с частичными размерами: рисунок не в масштабе, помещения выровнены по подписанным размерам мебели и проходов; контрольный обмер не выполнен (К-1); высота потолка 2700 мм принята: на плане заказчика её нет (К-2); толщины стен 300 / 120 мм приняты по плану заказчика, не замерены (К-1); разрешённая мощность 15 кВт принята по типовым ТУ для квартиры, ТУ заказчиком не переданы (К-4); подрайон климата не задан — принят не северный (жилые от 2,5 м) (К-6). См. лист открытых вопросов (лист 6, записи К-1, К-2, К-4, К-6).

1000 мм · печать 1:1

Изм.	Кол.уч	Лист	№ док.	Подп.	Дата
Разраб.		Кырлан А.С.			04.11.26
Пров.					
ГИП					
Н. контр.					
Утв.					

ГД-2026-008-АИ

Квартира с кабинетом

Общая площадь 127,29* м² · * размеры со скана, не замерены (реестр — л. 6–8, К-1)

Дизайн-проект интерьера	Стадия	Лист	Листов
	РП	106	131

Развёртка стены В. Кухня-гостиная (пом. 4)

М 1:25


Кырлан Александр Сергеевич

выпуск 04.11.2026 № 4177cbe7a3 · стр. 115 из 166

Развёртка стены В: схема и ведомость отделки. Кухня-гостиная (пом. 4)

Кухня-гостиная (пом. 4) · к развёртке на листе 106

Схема развёрток (М 1:50)

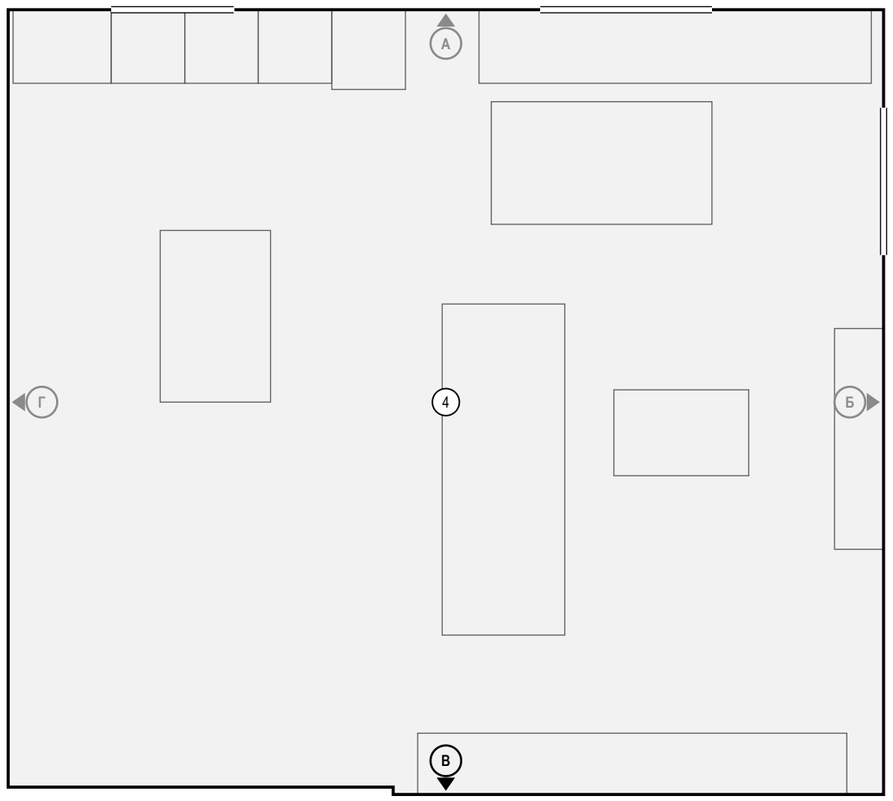

Условные обозначения

- мебель и приборы — фасад по расстановке (условно)
- дверной проём; марка двери — в кружке
- стены и перекрытия в сечении
- окраска: тон — цвет по коду производителя (условно)
- О1 — марка отделки по реестру отделки альбома
- А — марка развёртки: буква стены, стрелка — взгляд

Ведомость отделки (на листе)

Марка	Поверхность	Материал, изделие	Цвет, код	Кол.
О1	стены	окраска, Farrow & Ball Modern Emulsion, матовая, подготовка Q3	Farrow & Ball No. 15 «Bone — мягкий каменно-серый с зеленцой»	16 м²
О3	плинтус	плинтус МДФ, h 80 мм, аналог: плинтус МДФ под покраску 80×16	Farrow & Ball No. 15 «Bone — мягкий каменно-серый с зеленцой»	2,4 м
О4	потолок	окраска, Tikkurila Anti-Reflex 2, глубокоматовая, подготовка Q3	Tikkurila V503 «Winter»	45,5 м²

Примечания

1. Схема, условные обозначения и ведомость отделки — к развёртке стены В на листе 106: вид в своём масштабе занимает лист целиком.
2. Расположение развёрток всех помещений — на листе 85; полная ведомость отделки — на листах отделочника.

Допущения и предложения на листе

Основа листа: размеры сняты с растрового плана заказчика с частичными размерами: рисунок не в масштабе, помещения выровнены по подписанным размерам мебели и проходов; контрольный обмер не выполнен (К-1); высота потолка 2700 мм принята: на плане заказчика её нет (К-2); толщины стен 300 / 120 мм приняты по плану заказчика, не замерены (К-1); разрешённая мощность 15 кВт принята по типовым ТУ для квартиры, ТУ заказчиком не переданы (К-4); подрайон климата не задан — принят не северный (жилые от 2,5 м) (К-6). Знак «**» — предложение проектировщика, заказчиком не утверждено (согласовать с заказчиком): плинтус пом. 4, фартук пом. 4 — артикул изделия не выбран: позиция описана характеристиками («аналог по характеристикам»), артикул выбирается при закупке.

См. лист открытых вопросов (лист 6, записи К-1, К-2, К-4, К-6).

Изм.	Кол.уч	Лист	№ док.	Подп.	Дата
Разраб.		Кырлан А.С.			04.11.26
Пров.					
ГИП					
Н. контр.					
Утв.					

ГД-2026-008-АИ

Квартира с кабинетом

Общая площадь 127,29* м² · * размеры со скана, не замерены (реестр — л. 6–8, К-1)

Дизайн-проект интерьера

Стадия	Лист	Листов
РП	107	131

Развёртка стены В: схема и ведомость отделки. Кухня-гостиная (пом. 4)

М б/м


Кырлан Александр Сергеевич

Развёртки стен А1, А2. Коридор (пом. 5)

Коридор (пом. 5) · вид изнутри помещения · размеры в мм, отметки в м


ПРЕДВАРИТЕЛЬНО · не для производства работ · открыто пунктов: 13 (реестр — л. 6–8)

Развёртка стены А1

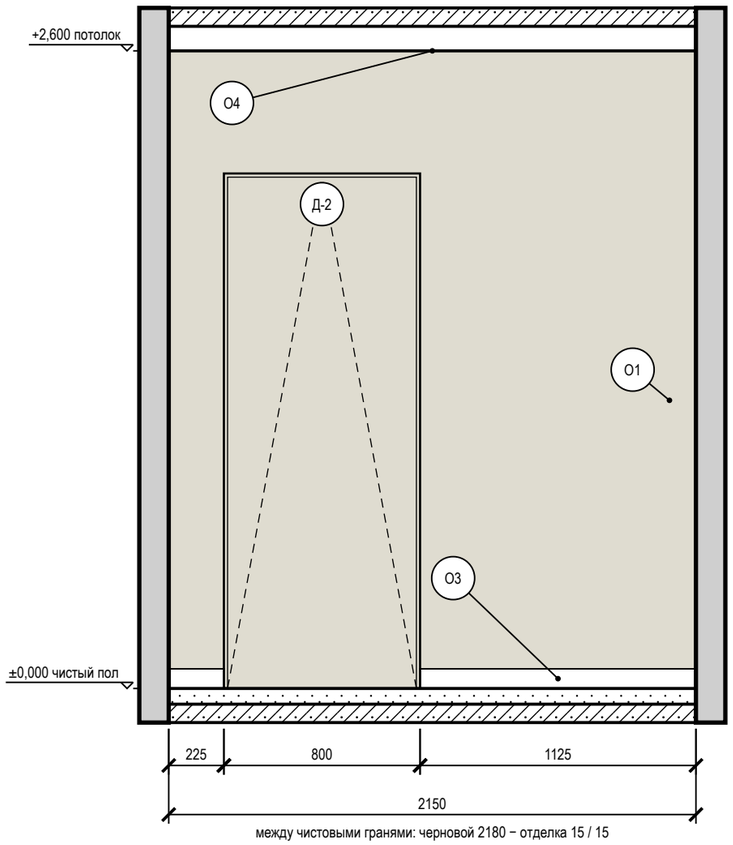


между чистовыми гранями: черновой 2180 − отделка 15 / 15

Развёртка стены А2

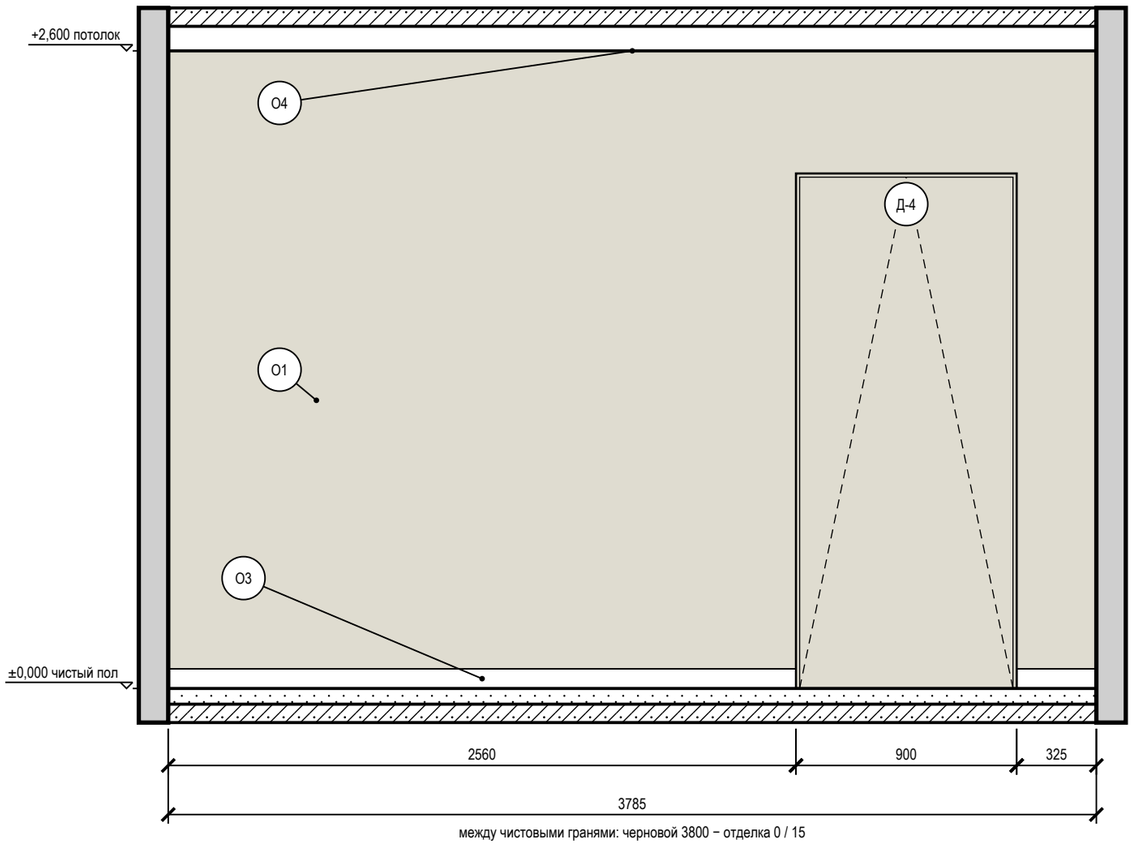

между чистовыми гранями: черновой 3800 − отделка 0 / 15

Схема развёрток (М 1:100)

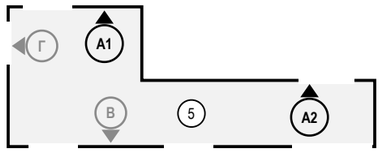

Условные обозначения

- мебель и приборы — фасад по расстановке (условно)
- дверь скрытого монтажа: полотно в плоскости стены (узел — на листе узлов)
- стены и перекрытия в сечении
- окраска: тон — цвет по коду производителя (условно)
- О1 — марка отделки по реестру отделки альбома
- А — марка развёртки: буква стены, стрелка — взгляд

Ведомость отделки (на листе)

Марка	Поверхность	Материал, изделие	Цвет, код	Кол.
О1	стены	окраска, Farrow & Ball Modern Emulsion, матовая, подготовка Q3	Farrow & Ball No. 15 «Bone — мягкий каменно-серый с зеленцой»	11,9 м²
О3	плинтус	плинтус МДФ, h 80 мм, аналог: плинтус МДФ под покраску 80×16	Farrow & Ball No. 15 «Bone — мягкий каменно-серый с зеленцой»	4,2 м
О4	потолок	окраска, Tikkurila Anti-Reflex 2, глубокоматовая, подготовка Q3	Tikkurila V503 «Winter»	9,1 м²

Примечания

1. Развёртки — вид на стену изнутри помещения, по часовой стрелке; расположение — на схеме листа и на листе 85; размеры — в мм по чистовым поверхностям; отметки — в м от ±0,000; высоты Н — от чистого пола помещения до оси изделия, у декора — до центра.
2. Схема мебели, приборов и декора не является технической документацией для производства мебели; габариты — по паспортам изделий.
3. Двери скрытого монтажа — полотно в плоскости стены, отделка стены по полотну, плинтус прерывается у короба (узел — на листе узлов).

Допущения и предложения на листе

Основа листа: размеры сняты с растрового плана заказчика с частичными размерами: рисунок не в масштабе, помещения выровнены по подписанным размерам мебели и проходов; контрольный обмер не выполнен (К-1); высота потолка 2700 мм принята: на плане заказчика её нет (К-2); толщины стен 300 / 120 мм приняты по плану заказчика, не замерены (К-1); разрешённая мощность 15 кВт принята по типовым ТУ для квартиры, ТУ заказчиком не переданы (К-4); подрайон климата не задан — принят не северный (жилые от 2,5 м) (К-6). См. лист открытых вопросов (лист 6, записи К-1, К-2, К-4, К-6).

1000 мм · печать 1:1

Изм.	Кол.уч	Лист	№ док.	Подп.	Дата
Разраб.		Кырлан А.С.			04.11.26
Пров.					
ГИП					
Н. контр.					
Утв.					

ГД-2026-008-АИ

Квартира с кабинетом

Общая площадь 127,29* м² · * размеры со скана, не замерены (реестр — л. 6–8, К-1)

Дизайн-проект интерьера

Стадия	Лист	Листов
РП	108	131

Развёртки стен А1, А2. Коридор (пом. 5)

М 1:25

Кырлан Александр Сергеевич


выпуск 04.11.2026 № 4177cbe7a3 · стр. 117 из 166

Развёртка стены В. Коридор (пом. 5)

Коридор (пом. 5) · вид изнутри помещения · размеры в мм, отметки в м

ПРЕДВАРИТЕЛЬНО · не для производства работ · открыто пунктов: 13 (реестр — л. 6–8)

Развёртка стены В

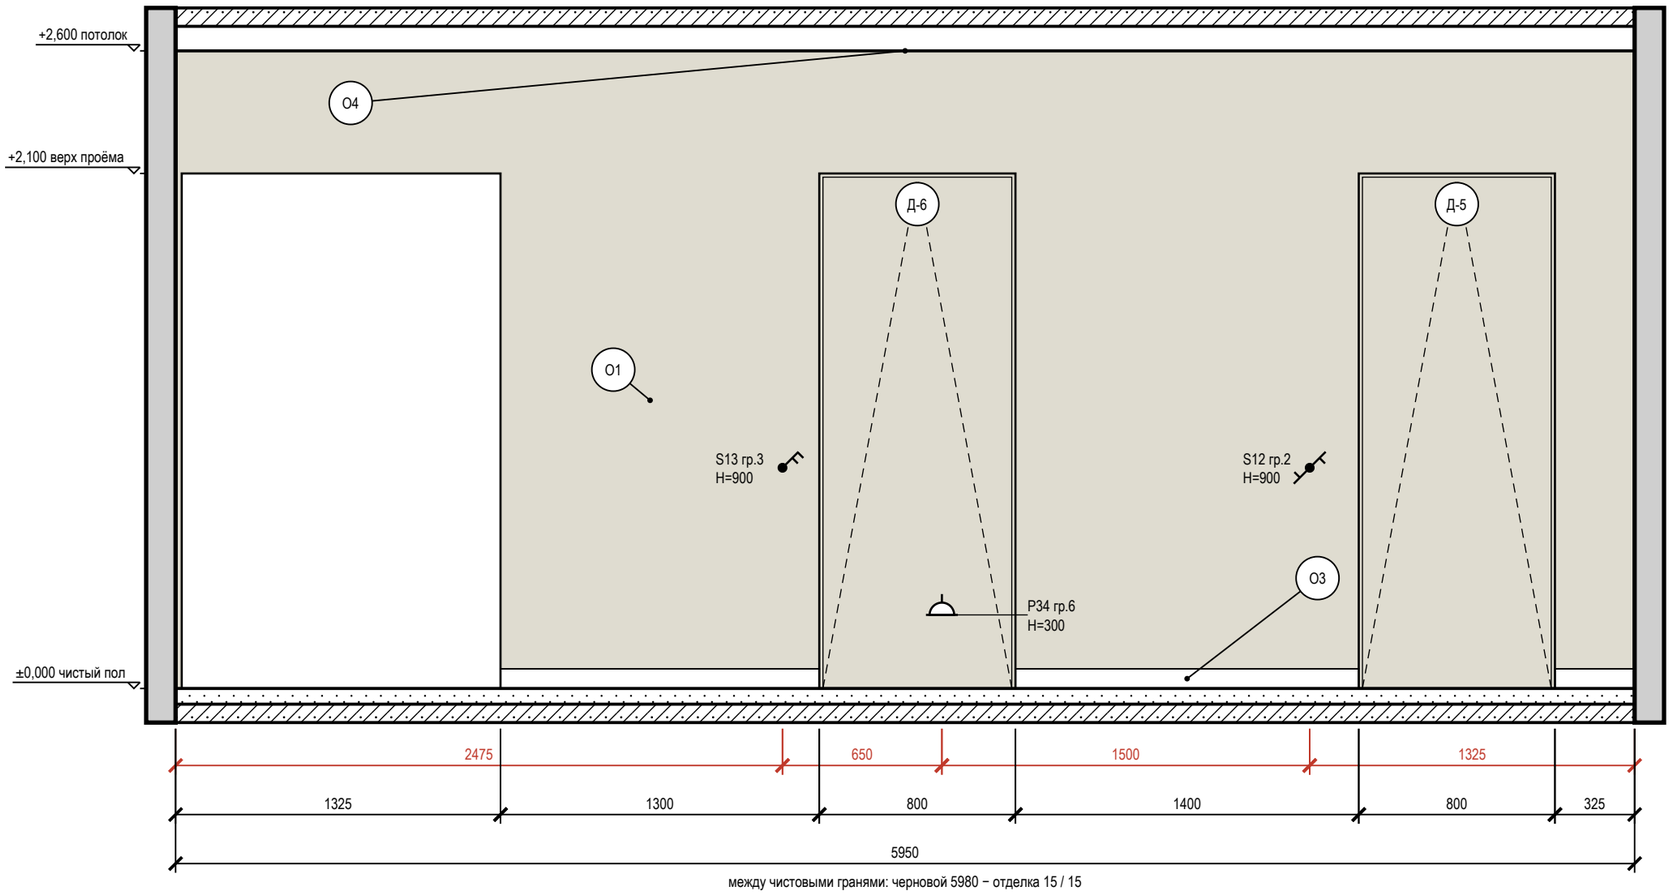


между чистовыми гранями: черновой 5980 − отделка 15 / 15

Условные обозначения

- розетка с заземляющим контактом; у знака — марка, ×N постов в рамке, гр. — группа щита, H — высота оси, мм
- выключатель одноклавишный
- выключатель двухклавишный (флажков — по числу клавиш)
- выключатель с проходной или перекрёстной клавишей (обратный флажок); тип клавиши — в подписи
- привязки точек и выводов от угла и от пола, мм
- мебель и приборы — фасад по расстановке (условно)
- дверь скрытого монтажа: полотно в плоскости стены (узел — на листе узлов)
- дверной проём; марка двери — в кружке
- стены и перекрытия в сечении
- окраска: тон — цвет по коду производителя (условно)
- О1 — марка отделки по реестру отделки альбома
- A — марка развёртки: буква стены, стрелка — взгляд

Схема развёрток (М 1:100)

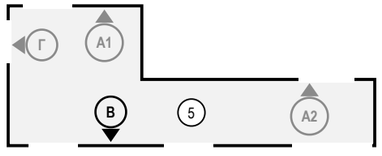

Ведомость отделки (на листе)

Марка	Поверхность	Материал, изделие	Цвет, код	Кол.
О1	стены	окраска, Farrow & Ball Modern Emulsion, матовая, подготовка Q3	Farrow & Ball No. 15 «Bone — мягкий каменно-серый с зеленцой»	9,4 м²
О3	плинтус	плинтус МДФ, h 80 мм, аналог: плинтус МДФ под покраску 80×16	Farrow & Ball No. 15 «Bone — мягкий каменно-серый с зеленцой»	3 м
О4	потолок	окраска, Tikkurila Anti-Reflex 2, глубокоматовая, подготовка Q3	Tikkurila V503 «Winter»	9,1 м²

Допущения и предложения на листе

Основа листа: размеры сняты с растрового плана заказчика с частичными размерами: рисунок не в масштабе, помещения выровнены по подписанным размерам мебели и проходов; контрольный обмер не выполнен (К-1); высота потолка 2700 мм принята: на плане заказчика её нет (К-2); толщины стен 300 / 120 мм приняты по плану заказчика, не замерены (К-1); разрешённая мощность 15 кВт принята по типовым ТУ для квартиры, ТУ заказчиком не переданы (К-4); подрайон климата не задан — принят не северный (жилые от 2,5 м) (К-6).

См. лист открытых вопросов (лист 6, записи К-1, К-2, К-4, К-6).

Примечания

1. Развёртки — вид на стену изнутри помещения, по часовой стрелке; расположение — на схеме листа и на листе 85; размеры — в мм по чистовым поверхностям; отметки — в м от ±0,000; высоты H — от чистого пола помещения до оси изделия, у декора — до центра.
2. Красная цепочка — привязки электроточек и выводов по осям от угла чистовых стен; высота H — у знака, от чистого пола до оси; высоты мебели, проёмов и границ отделки — колонкой отметок слева. Стена с 5 и более точками или с мелкими звеньями привязок показана двумя видами: архитектурная развёртка (мебель, отделка, проёмы, высоты) и вид «Привязки» на отдельном листе — точки и выводы с марками, одна цепочка по осям и таблица привязок (каждая точка — строка).
3. У знака электроточки: марка (Р — розетка, S — выключатель, Св — светильник, ЭВ — вывод кабеля), ×N — число постов в рамке, гр. — группа щита, H — высота оси от чистого пола, мм; группы по клавишам выключателя — на листе выключателей.
4. Схема мебели, приборов и декора не является технической документацией для производства мебели; габариты — по паспортам изделий.
5. Двери скрытого монтажа — полотно в плоскости стены, отделка стены по полотну, плинтус прерывается у короба (узел — на листе узлов).

1000 мм · печать 1:1

Изм.	Кол.уч	Лист	№ док.	Подп.	Дата
Разраб.		Кырлан А.С.			04.11.26
Пров.					
ГИП					
Н. контр.					
Утв.					

ГД-2026-008-АИ

Квартира с кабинетом

Общая площадь 127,29* м² · * размеры со скана, не замерены (реестр — л. 6–8, К-1)

Дизайн-проект интерьера

Стадия	Лист	Листов
РП	109	131

Развёртка стены В. Коридор (пом. 5)

М 1:25

Кырлан Александр Сергеевич

выпуск 04.11.2026 № 4177cbe7a3 · стр. 118 из 166

Развёртка стены Г. Коридор (пом. 5)

Коридор (пом. 5) · вид изнутри помещения · размеры в мм, отметки в м

ПРЕДВАРИТЕЛЬНО · не для производства работ · открыто пунктов: 13 (реестр — л. 6–8)

Развёртка стены Г


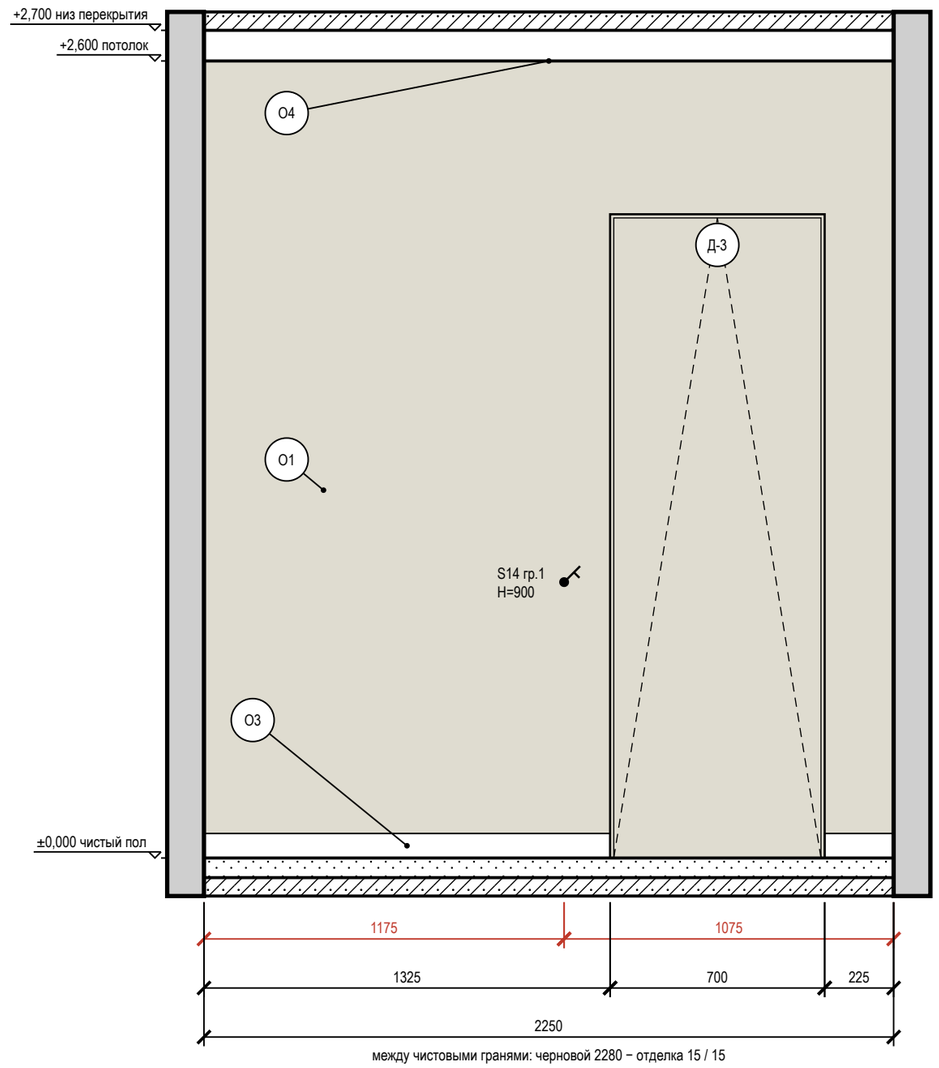


Схема развёрток (М 1:100)

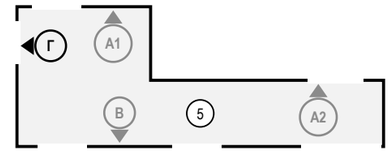

Условные обозначения

- выключатель одноклавишный
- привязки точек и выводов от угла и от пола, мм
- мебель и приборы — фасад по расстановке (условно)
- дверь скрытого монтажа: полотно в плоскости стены (узел — на листе узлов)
- стены и перекрытия в сечении
- окраска: тон — цвет по коду производителя (условно)
- О1 — марка отделки по реестру отделки альбома
- А — марка развёртки: буква стены, стрелка — взгляд

Ведомость отделки (на листе)

Марка	Поверхность	Материал, изделие	Цвет, код	Кол.
О1	стены	окраска, Farrow & Ball Modern Emulsion, матовая, подготовка Q3	Farrow & Ball No. 15 «Bone — мягкий каменно-серый с зеленцой»	4,4 м²
О3	плинтус	плинтус МДФ, h 80 мм, аналог: плинтус МДФ под покраску 80×16	Farrow & Ball No. 15 «Bone — мягкий каменно-серый с зеленцой»	1,6 м
О4	потолок	окраска, Tikkurila Anti-Reflex 2, глубокоматовая, подготовка Q3	Tikkurila V503 «Winter»	9,1 м²

Допущения и предложения на листе

Основа листа: размеры сняты с растрового плана заказчика с частичными размерами: рисунок не в масштабе, помещения выровнены по подписанным размерам мебели и проходов; контрольный обмер не выполнен (К-1); высота потолка 2700 мм принята: на плане заказчика её нет (К-2); толщины стен 300 / 120 мм приняты по плану заказчика, не замерены (К-1); разрешённая мощность 15 кВт принята по типовым ТУ для квартиры, ТУ заказчиком не переданы (К-4); подрайон климата не задан — принят не северный (жилые от 2,5 м) (К-6).
См. лист открытых вопросов (лист 6, записи К-1, К-2, К-4, К-6).

Примечания

1. Развёртки — вид на стену изнутри помещения, по часовой стрелке; расположение — на схеме листа и на листе 85; размеры — в мм по чистовым поверхностям; отметки — в м от ±0,000; высоты Н — от чистого пола помещения до оси изделия, у декора — до центра.
2. Красная цепочка — привязки электроточек и выводов по осям от угла чистовых стен; высота Н — у знака, от чистого пола до оси; высоты мебели, проёмов и границ отделки — колонкой отметок слева. Стена с 5 и более точками или с мелкими звеньями привязок показана двумя видами: архитектурная развёртка (мебель, отделка, проёмы, высоты) и вид «Привязки» на отдельном листе — точки и выводы с марками, одна цепочка по осям и таблица привязок (каждая точка — строка).
3. У знака электроточки: марка (Р — розетка, S — выключатель, Св — светильник, ЭВ — вывод кабеля), ×N — число постов в рамке, гр. — группа щита, Н — высота оси от чистого пола, мм; группы по клавишам выключателя — на листе выключателей.
4. Схема мебели, приборов и декора не является технической документацией для производства мебели; габариты — по паспортам изделий.
5. Двери скрытого монтажа — полотно в плоскости стены, отделка стены по полотну, плинтус прерывается у короба (узел — на листе узлов).

1000 мм · печать 1:1

Изм.	Кол.уч	Лист	№ док.	Подп.	Дата
Разраб.		Кырлан А.С.			04.11.26
Пров.					
ГИП					
Н. контр.					
Утв.					

ГД-2026-008-АИ

Квартира с кабинетом

Общая площадь 127,29* м² · * размеры со скана, не замерены (реестр — л. 6–8, К-1)

Дизайн-проект интерьера

Стадия	Лист	Листов
РП	110	131

Развёртка стены Г. Коридор (пом. 5)

М 1:20

Кырлан Александр Сергеевич


выпуск 04.11.2026 № 4177cbe7a3 · стр. 119 из 166

Развёртки стен А, Б. Детская (пом. 6)

Детская (пом. 6) · вид изнутри помещения · размеры в мм, отметки в м


ПРЕДВАРИТЕЛЬНО · не для производства работ · открыто пунктов: 13 (реестр — л. 6–8)

Развёртка стены А

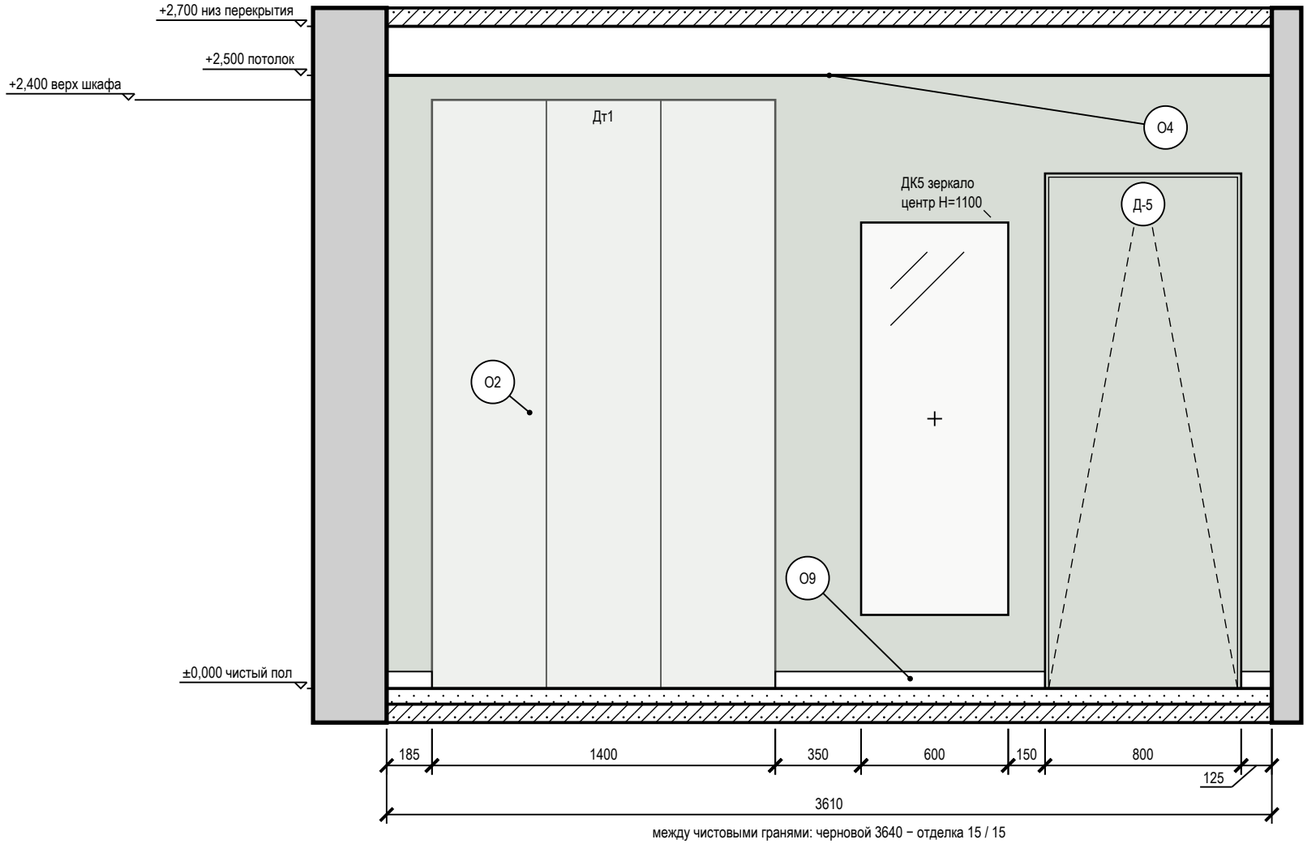


между чистовыми гранями: черновой 3640 − отделка 15 / 15

Развёртка стены Б

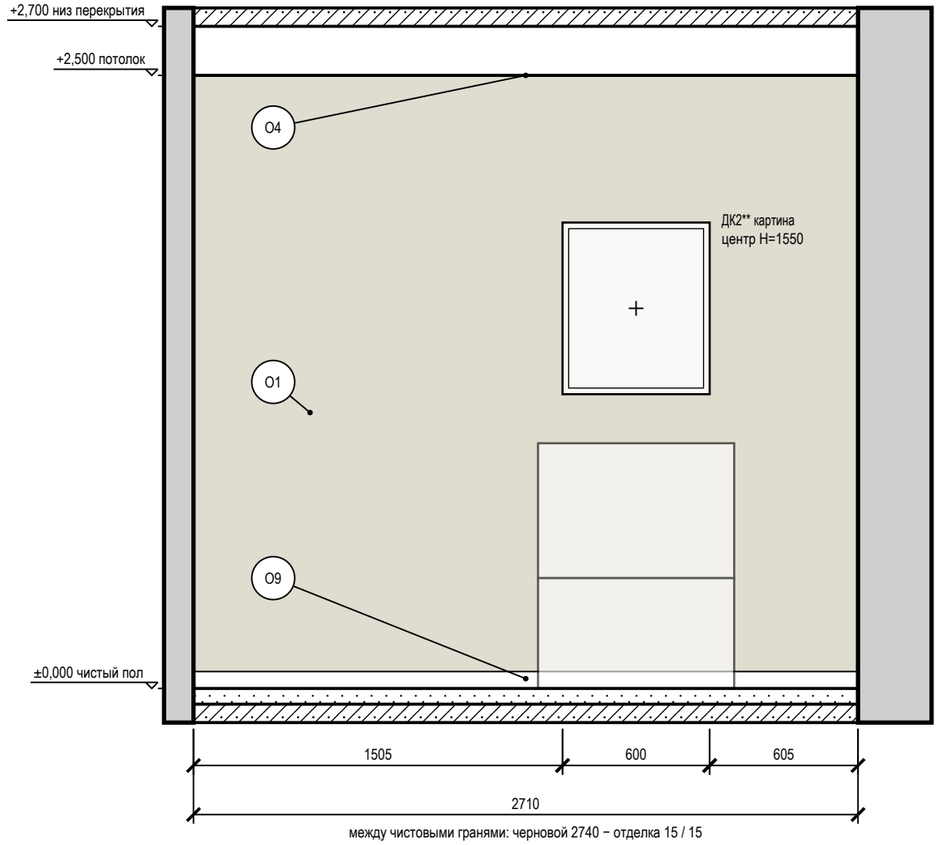

между чистовыми гранями: черновой 2740 − отделка 15 / 15

Схема развёрток (М 1:100)

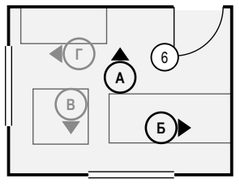

Условные обозначения

- мебель и приборы — фасад по расстановке (условно)
- картина (декор): марка Д, крест — центр, Н — высота центра, мм
- зеркало: марка Д, крест — центр, Н — высота центра, мм
- дверь скрытого монтажа: полотно в плоскости стены (узел — на листе узлов)
- стены и перекрытия в сечении
- окраска: тон — цвет по коду производителя (условно)
- О1 — марка отделки по реестру отделки альбома
- А — марка развёртки: буква стены, стрелка — взгляд

Допущения и предложения на листе

Основа листа: размеры сняты с растрового плана заказчика с частичными размерами: рисунок не в масштабе, помещения выровнены по подписанным размерам мебели и проходов; контрольный обмер не выполнен (К-1); высота потолка 2700 мм принята: на плане заказчика её нет (К-2); толщины стен 300 / 120 мм приняты по плану заказчика, не замерены (К-1); разрешённая мощность 15 кВт принята по типовым ТУ для квартиры, ТУ заказчиком не переданы (К-4); подрайон климата не задан — принят не северный (жилые от 2,5 м) (К-6).
Знак «**» — предложение проектировщика, заказчиком не утверждено (согласовать с заказчиком): ИЗ-1: ДК2 — низ 1200 = верх изголовья Дт2 1000 + 200 (150–250 над изголовьем, не над матрасом).
См. лист открытых вопросов (лист 6, записи К-1, К-2, К-4, К-6; лист 7, запись ИЗ-1).

Примечания

1. Развёртки — вид на стену изнутри помещения, по часовой стрелке; расположение — на схеме листа и на листе 85; размеры — в мм по чистовым поверхностям; отметки — в м от ±0,000; высоты Н — от чистого пола помещения до оси изделия, у декора — до центра.
2. Стена Б показана двумя видами: здесь — архитектурная развёртка (мебель, отделка, проёмы, высоты), электроточки и выводы ВК с привязками и таблицей — на листе 112 («Привязки»).
3. Схема мебели, приборов и декора не является технической документацией для производства мебели; габариты — по паспортам изделий.
4. Картины и зеркала крепить к основанию по паспорту изделия (закладные и анкеры — в перечне скрытых работ); крест — ось центра предмета.
5. Двери скрытого монтажа — полотно в плоскости стены, отделка стены по полотну, плинтус прерывается у короба (узел — на листе узлов).
6. Потолок — у каждой стены свой, по плану потолков (ПТ1); ступени — зоной, кромка короба перед нишей — тонкой линией; в поле потолка: ПТ2 +2,600.

1000 мм · печать 1:1

Изм.	Кол.уч	Лист	№ док.	Подп.	Дата
Разраб.		Кырлан А.С.			04.11.26
Пров.					
ГИП					
Н. контр.					
Утв.					

ГД-2026-008-АИ

Квартира с кабинетом

Общая площадь 127,29* м² · * размеры со скана, не замерены (реестр — л. 6–8, К-1)

Дизайн-проект интерьера

Стадия	Лист	Листов
РП	111	131

Развёртки стен А, Б. Детская (пом. 6)

М 1:25

Кырлан Александр Сергеевич

выпуск 04.11.2026 № 4177cbe7a3 · стр. 120 из 166

Привязки электроточек, стена Б. Детская (пом. 6)

Детская (пом. 6) · вид изнутри помещения · привязки в мм, отметки в м · к развёртке на листе 111

ПРЕДВАРИТЕЛЬНО · не для производства работ · открыто пунктов: 13 (реестр — л. 6–8)

Развёртка стены Б: электроточки и выводы

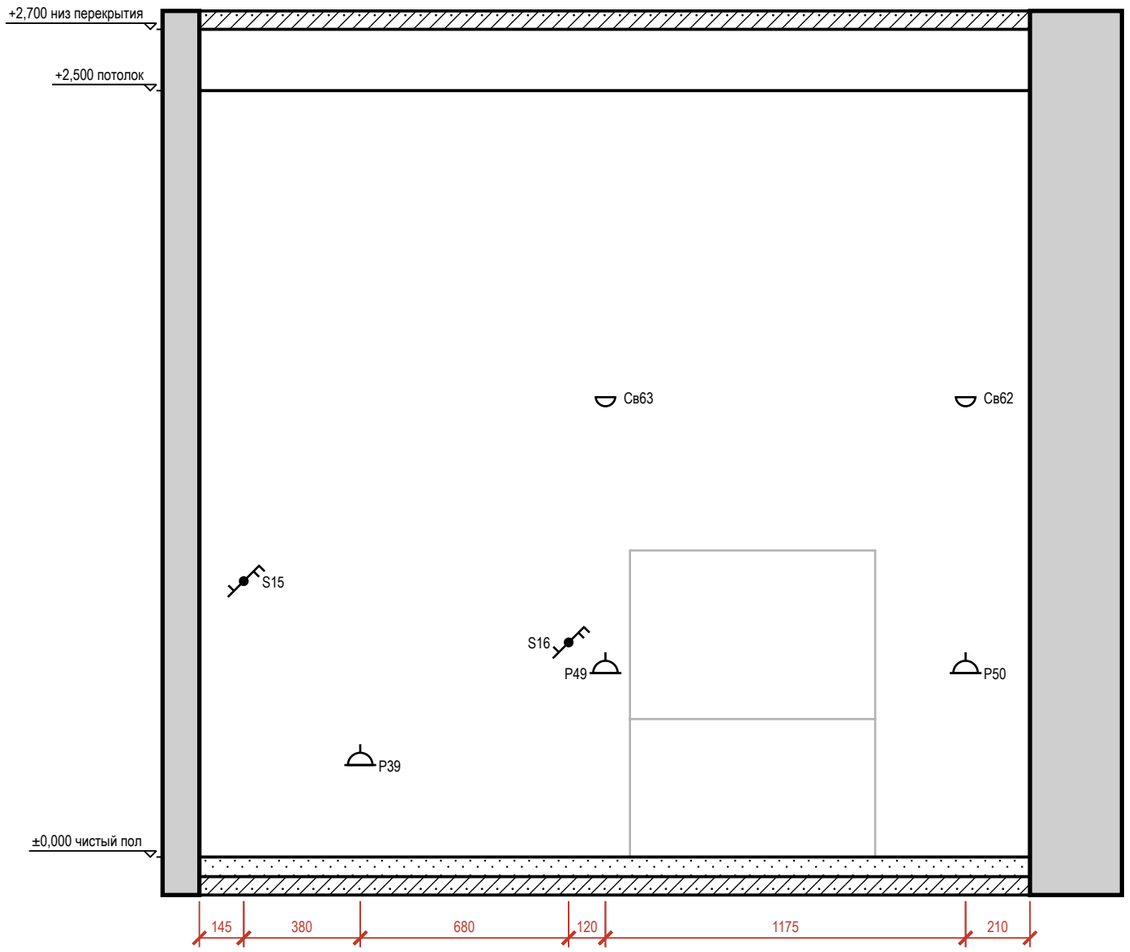



Таблица привязок электроточек и выводов

Марка	Назначение	От угла, мм	Н от пола, мм	Примечание
S15	выключатель	145	900	гр. 1
P39	розетка: уборка	525	300	гр. 5
S16	выключатель	1205	700	гр. 1
P49	розетка: у кровати	1325	600	гр. 5
Св63	светильник настенный	1325	1500	гр. 1
P50	розетка: у кровати	2500	600	гр. 5
Св62	светильник настенный	2500	1500	гр. 1

Условные обозначения

- розетка с заземляющим контактом; у знака — марка, ×N постов в рамке, гр. — группа щита, Н — высота оси, мм
- выключатель одноклавишный
- выключатель двухклавишный (флажков — по числу клавиш)
- выключатель с проходной или перекрёстной клавишей (обратный флажок); тип клавиши — в подписи
- светильник настенный (бра), Н — высота оси
- привязки точек и выводов от угла и от пола, мм
- марка развёртки: буква стены, стрелка — взгляд

Схема развёрток (М 1:50)

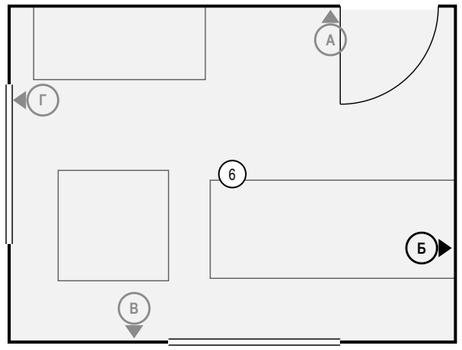

Примечания

1. Вид «Привязки» стены Б — электроточки и выводы ВК; архитектурная развёртка (мебель, отделка, проёмы, высоты) — на листе 111, расположение — на листе 85. Мебель и приборы — подложкой для ориентира; их марки и обозначения мебели, проёмов и стен — там же.
2. Привязки — в мм: по горизонтали от левого чистового угла стены до оси изделия, Н — от чистого пола до оси; все точки — в таблице привязок. Красная цепочка — привязки по осям; точки ближе 120 мм одна к другой в цепочку не дробятся — их привязки только в таблице.
3. У знака — марка электроточки (Р — розетка, S — выключатель, Св — светильник, ЭВ — вывод кабеля); посты в рамке и группа щита — в графе «Примечание»; группы по клавишам выключателя — на листе выключателей.

Допущения и предложения на листе

Основа листа: размеры сняты с растрового плана заказчика с частичными размерами: рисунок не в масштабе, помещения выровнены по подписанным размерам мебели и проходов; контрольный обмер не выполнен (К-1); высота потолка 2700 мм принята: на плане заказчика её нет (К-2); толщины стен 300 / 120 мм приняты по плану заказчика, не замерены (К-1); разрешённая мощность 15 кВт принята по типовым ТУ для квартиры, ТУ заказчиком не переданы (К-4); подрайон климата не задан — принят не северный (жилые от 2,5 м) (К-6). См. лист открытых вопросов (лист 6, записи К-1, К-2, К-4, К-6).

1000 мм · печать 1:1

Изм.	Кол.уч	Лист	№ док.	Подп.	Дата
Разраб.		Кырлан А.С.			04.11.26
Пров.					
ГИП					
Н. контр.					
Утв.					

ГД-2026-008-АИ

Квартира с кабинетом

Общая площадь 127,29* м² · * размеры со скана, не замерены (реестр — л. 6–8, К-1)

Дизайн-проект интерьера	Стадия	Лист	Листов
	РП	112	131
Привязки электроточек, стена Б. Детская (пом. 6) М 1:20	**Кырлан Александр Сергеевич**		


выпуск 04.11.2026 № 4177cbe7a3 · стр. 121 из 166

Развёртка стены В. Детская (пом. 6)

Детская (пом. 6) · вид изнутри помещения · размеры в мм, отметки в м


ПРЕДВАРИТЕЛЬНО · не для производства работ · открыто пунктов: 13 (реестр — л. 6–8)

Развёртка стены В

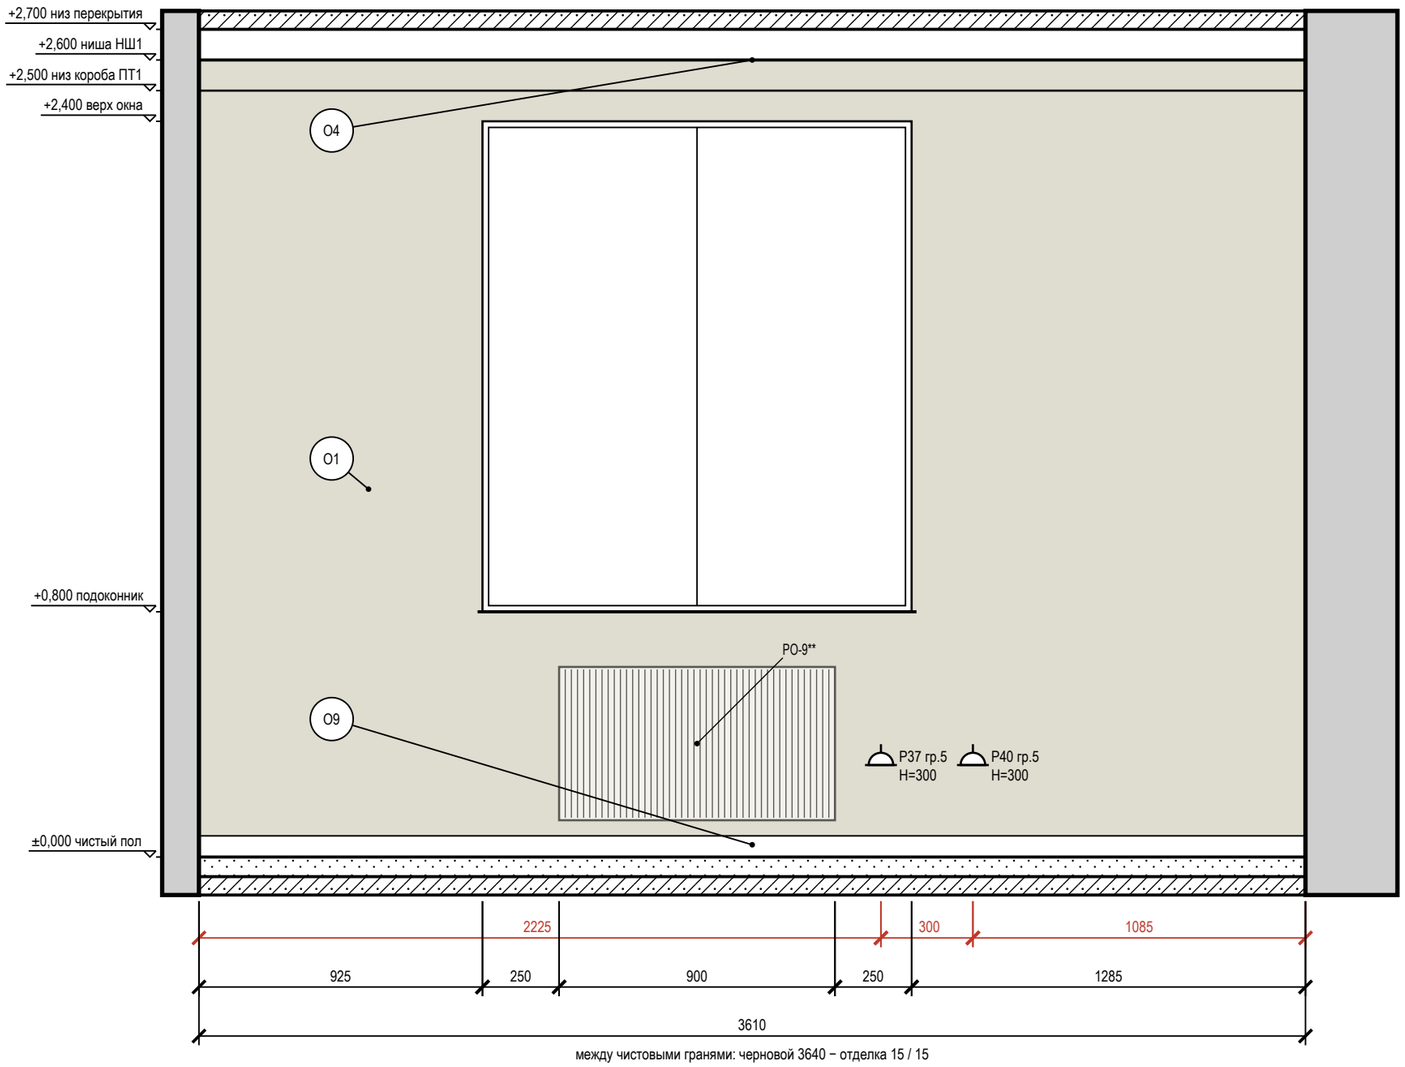

между чистовыми гранями: черновой 3640 − отделка 15 / 15

Схема развёрток (М 1:100)

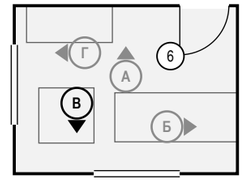

Условные обозначения

- розетка с заземляющим контактом; у знака — марка, ×N постов в рамке, гр. — группа щита, Н — высота оси, мм
- привязки точек и выводов от угла и от пола, мм
- мебель и приборы — фасад по расстановке (условно)
- окно: проём, рама, подоконник
- радиатор отопления; марка — по плану отопления
- стены и перекрытия в сечении
- окраска: тон — цвет по коду производителя (условно)
- О1 — марка отделки по реестру отделки альбома
- А — марка развёртки: буква стены, стрелка — взгляд

Ведомость отделки (на листе)

Марка	Поверхность	Материал, изделие	Цвет, код	Кол.
О1	стены	окраска, Farrow & Ball Modern Emulsion, матовая, подготовка Q3	Farrow & Ball No. 15 «Bone — мягкий каменно-серый с зеленцой»	7,1 м²
О4	потолок	окраска, Tikkurila Anti-Reflex 2, глубокоматовая, подготовка Q3	Tikkurila V503 «Winter»	10 м²
О9	плинтус	плинтус МДФ, Orac Decor Contour (Luxxus), h 69 мм, SX165	Farrow & Ball No. 15 «Bone — мягкий каменно-серый с зеленцой»	3,6 м

Допущения и предложения на листе

Основа листа: размеры сняты с растрового плана заказчика с частичными размерами: рисунок не в масштабе, помещения выровнены по подписанным размерам мебели и проходов; контрольный обмер не выполнен (К-1); высота потолка 2700 мм принята: на плане заказчика её нет (К-2); толщины стен 300 / 120 мм приняты по плану заказчика, не замерены (К-1); разрешённая мощность 15 кВт принята по типовым ТУ для квартиры, ТУ заказчиком не переданы (К-4); подрайон климата не задан — принят не северный (жилые от 2,5 м) (К-6).
Знак «**» — предложение проектировщика, заказчиком не утверждено (согласовать с заказчиком): К-1: РО-9 — прибор под окном по оси проёма, ширина ≈ 0,7 ширины окна — предложение ОВ (лист ОВ выводил его сам до, теперь он в данных — один источник для листа, мебели, DXF и IFC); стояки и подводки отопления не замерены, мощность — по теплотехническому расчёту ОВ.
См. лист открытых вопросов (лист 6, записи К-1, К-2, К-4, К-6).

Примечания

1. Развёртки — вид на стену изнутри помещения, по часовой стрелке; расположение — на схеме листа и на листе 85; размеры — в мм по чистовым поверхностям; отметки — в м от ±0,000; высоты Н — от чистого пола помещения до оси изделия, у декора — до центра.
2. Красная цепочка — привязки электроточек и выводов по осям от угла чистовых стен; высота Н — у знака, от чистого пола до оси; высоты мебели, проёмов и границ отделки — колонкой отметок слева. Стена с 5 и более точками или с мелкими звеньями привязок показана двумя видами: архитектурная развёртка (мебель, отделка, проёмы, высоты) и вид «Привязки» на отдельном листе — точки и выводы с марками, одна цепочка по осям и таблица привязок (каждая точка — строка).
3. У знака электроточки: марка (Р — розетка, S — выключатель, Св — светильник, ЭВ — вывод кабеля), ×N — число постов в рамке, гр. — группа щита, Н — высота оси от чистого пола, мм; группы по клавишам выключателя — на листе выключателей.
4. Схема мебели, приборов и декора не является технической документацией для производства мебели; габариты — по паспортам изделий.
5. Потолок — у каждой стены свой, по плану потолков (НШ1, ПТ1); ступени — зоной, кромка короба перед нишей — тонкой линией; в поле потолка: ПТ2 +2,600.

1000 мм · печать 1:1

Изм.	Кол.уч	Лист	№ док.	Подп.	Дата
Разраб.		Кырлан А.С.			04.11.26
Пров.					
ГИП					
Н. контр.					
Утв.					

ГД-2026-008-АИ

Квартира с кабинетом

Общая площадь 127,29* м² · * размеры со скана, не замерены (реестр — л. 6–8, К-1)

Дизайн-проект интерьера

Стадия	Лист	Листов
РП	113	131

Развёртка стены В. Детская (пом. 6)

М 1:20

Кырлан Александр Сергеевич

выпуск 04.11.2026 № 4177cbe7a3 · стр. 122 из 166

Развёртка стены Г. Детская (пом. 6)

Детская (пом. 6) · вид изнутри помещения · размеры в мм, отметки в м

ПРЕДВАРИТЕЛЬНО · не для производства работ · открыто пунктов: 13 (реестр — л. 6–8)

Развёртка стены Г


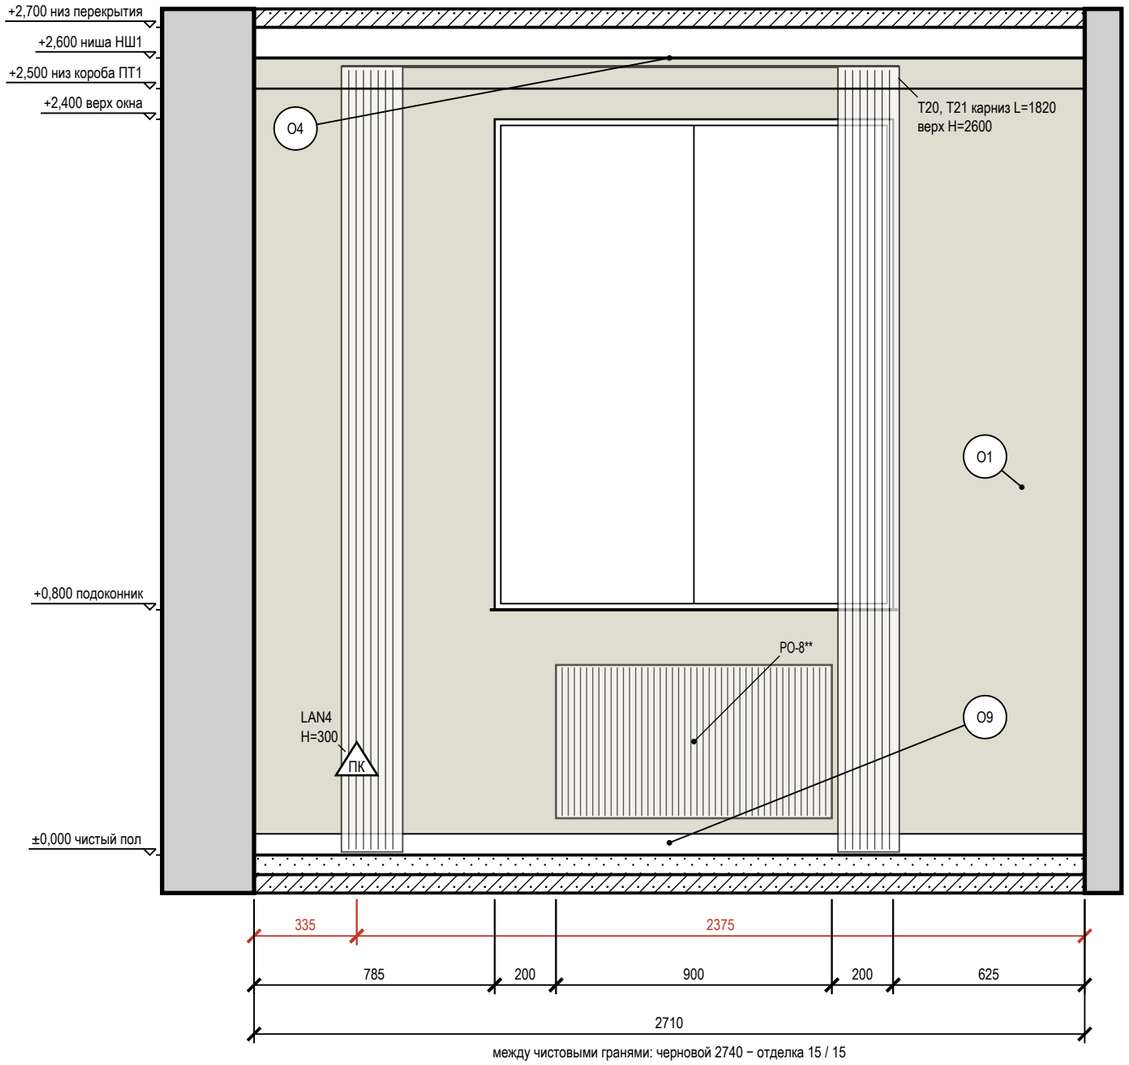


Схема развёрток (М 1:100)

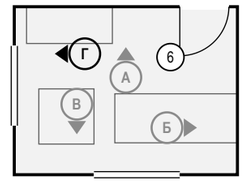

Условные обозначения

- ПК — розетка компьютерная RJ45
- привязки точек и выводов от угла и от пола, мм
- мебель и приборы — фасад по расстановке (условно)
- карниз (шина) и шторы в собранном виде: марка Т, длина L, верх H
- окно: проём, рама, подоконник
- радиатор отопления; марка — по плану отопления
- стены и перекрытия в сечении
- окраска: тон — цвет по коду производителя (условно)
- О1 — марка отделки по реестру отделки альбома
- А — марка развёртки: буква стены, стрелка — взгляд

Ведомость отделки (на листе)

Марка	Поверхность	Материал, изделие	Цвет, код	Кол.
О1	стены	окраска, Farrow & Ball Modern Emulsion, матовая, подготовка Q3	Farrow & Ball No. 15 «Bone — мягкий каменно-серый с зеленцой»	5 м²
О4	потолок	окраска, Tikkurila Anti-Reflex 2, глубокоматовая, подготовка Q3	Tikkurila V503 «Winter»	10 м²
О9	плинтус	плинтус МДФ, Orac Decor Contour (Luxxus), h 69 мм, SX165	Farrow & Ball No. 15 «Bone — мягкий каменно-серый с зеленцой»	2,7 м

Допущения и предложения на листе

Основа листа: размеры сняты с растрового плана заказчика с частичными размерами: рисунок не в масштабе, помещения выровнены по подписанным размерам мебели и проходов; контрольный обмер не выполнен (К-1); высота потолка 2700 мм принята: на плане заказчика её нет (К-2); толщины стен 300 / 120 мм приняты по плану заказчика, не замерены (К-1); разрешённая мощность 15 кВт принята по типовым ТУ для квартиры, ТУ заказчиком не переданы (К-4); подрайон климата не задан — принят не северный (жилые от 2,5 м) (К-6).

Знак «**» — предложение проектировщика, заказчиком не утверждено (согласовать с заказчиком): К-1: РО-8 — прибор под окном по оси проёма, ширина ≈ 0,7 ширины окна — предложение ОВ (лист ОВ выводил его сам до, теперь он в данных — один источник для листа, мебели, DXF и IFC); стояки и подводки отопления не замерены, мощность — по теплотехническому расчёту ОВ.

См. лист открытых вопросов (лист 6, записи К-1, К-2, К-4, К-6).

Примечания

1. Развёртки — вид на стену изнутри помещения, по часовой стрелке; расположение — на схеме листа и на листе 85; размеры — в мм по чистовым поверхностям; отметки — в м от ±0,000; высоты H — от чистого пола помещения до оси изделия, у декора — до центра.
2. Красная цепочка — привязки электроточек и выводов по осям от угла чистовых стен; высота H — у знака, от чистого пола до оси; высоты мебели, проёмов и границ отделки — колонкой отметок слева. Стена с 5 и более точками или с мелкими звеньями привязок показана двумя видами: архитектурная развёртка (мебель, отделка, проёмы, высоты) и вид «Привязки» на отдельном листе — точки и выводы с марками, одна цепочка по осям и таблица привязок (каждая точка — строка).
3. У знака электроточки: марка (Р — розетка, S — выключатель, Св — светильник, ЭВ — вывод кабеля), ×N — число постов в рамке, гр. — группа щита, H — высота оси от чистого пола, мм; группы по клавишам выключателя — на листе выключателей.
4. Схема мебели, приборов и декора не является технической документацией для производства мебели; габариты — по паспортам изделий.
5. Карнизы (шины) — по ведомости текстиля декоратора: длина L и верх H на развёртке — те же числа, что в ведомости; крепление — до окраски потолка.
6. Потолок — у каждой стены свой, по плану потолков (НШ1, ПТ1); ступени — зоной, кромка короба перед нишей — тонкой линией; в поле потолка: ПТ2 +2,600.

1000 мм · печать 1:1

Изм.	Кол.уч	Лист	№ док.	Подп.	Дата
Разраб.		Кырлан А.С.			04.11.26
Пров.					
ГИП					
Н. контр.					
Утв.					

ГД-2026-008-АИ

Квартира с кабинетом

Общая площадь 127,29* м² · * размеры со скана, не замерены (реестр — л. 6–8, К-1)

Дизайн-проект интерьера

Стадия	Лист	Листов
РП	114	131

Развёртка стены Г. Детская (пом. 6)

М 1:20

Кырлан Александр Сергеевич


выпуск 04.11.2026 № 4177cbe7a3 · стр. 123 из 166

Развёртки стен А, Б. Ванная (пом. 7)

Ванная (пом. 7) · вид изнутри помещения · размеры в мм, отметки в м


ПРЕДВАРИТЕЛЬНО · не для производства работ · открыто пунктов: 13 (реестр — л. 6–8)

Развёртка стены А

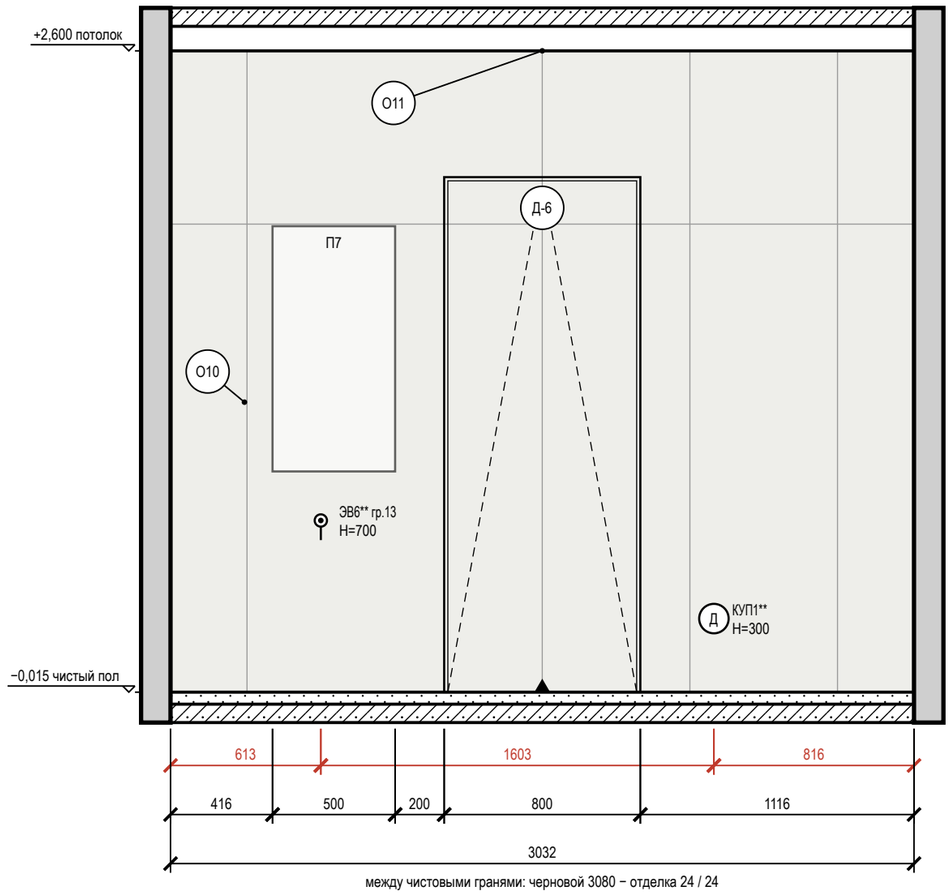


между чистовыми гранями: черновой 3080 − отделка 24 / 24

Развёртка стены Б

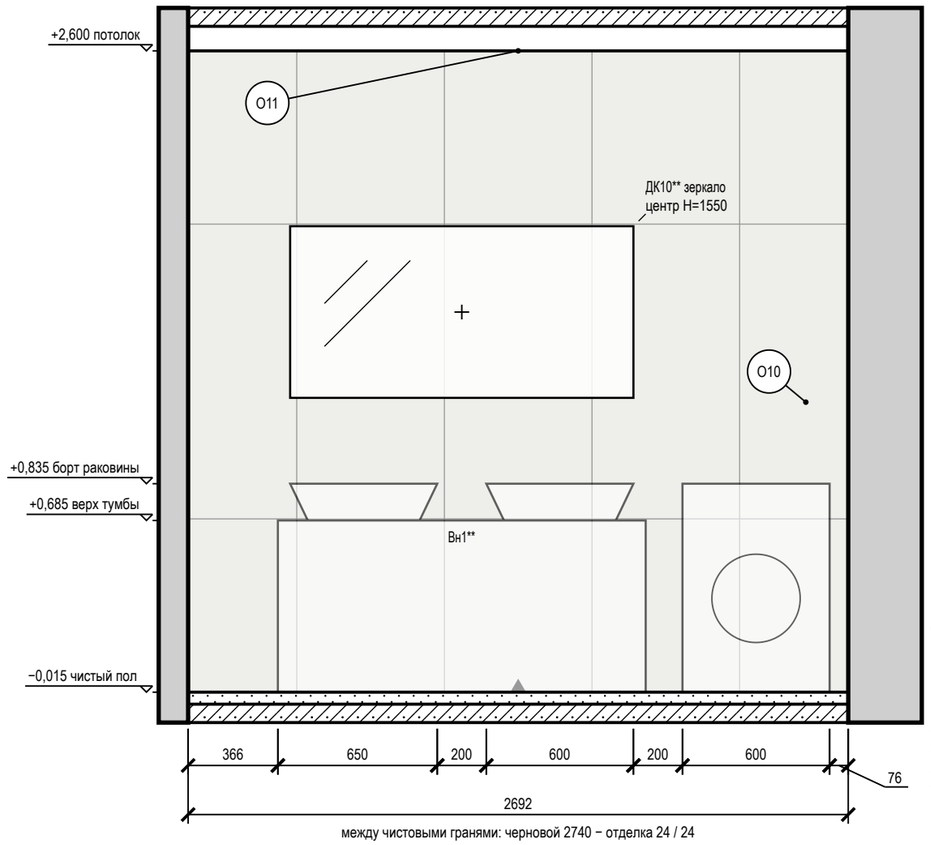

между чистовыми гранями: черновой 2740 − отделка 24 / 24

Схема развёрток (М 1:100)

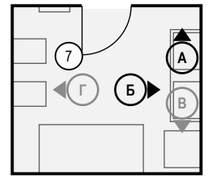

Допущения и предложения на листе. Основа листа: размеры сняты с растрового плана заказчика с частичными размерами: рисунок не в масштабе, помещения выровнены по подписанным размерам мебели и проходов; контрольный обмер не выполнен (К-1); высота потолка 2700 мм принята: на плане заказчика её нет (К-2); толщины стен 300 / 120 мм приняты по плану заказчика, не замерены (К-1); разрешённая мощность 15 кВт принята по типовым ТУ для квартиры, ТУ заказчиком не переданы (К-4); подрайон климата не задан — принят не северный (жилые от 2,5 м) (К-6). Знак «**» — предложено, не утверждено (согласовать): ДК10, ЭВ6; ИЗ-2: Вн1, КУП1; ИЗ-2, К-5: дверь пом. 7 (стена А). См. лист открытых вопросов (лист 6, записи К-1, К-2, К-4–К-6; лист 7, запись ИЗ-2).

Условные обозначения

- вывод кабеля для подключения прибора (без розетки), марка ЭВ
- привязки точек и выводов от угла и от пола, мм
- мебель и приборы — фасад по расстановке (условно)
- зеркало: марка Д, крест — центр, Н — высота центра, мм
- дверь скрытого монтажа: полотно в плоскости стены (узел — на листе узлов)
- стены и перекрытия в сечении
- плитка: сетка швов по формату, ▲ — ось старта
- О1 — марка отделки по реестру отделки альбома
- А — марка развёртки: буква стены, стрелка — взгляд

Примечания

1. Развёртки — вид на стену изнутри помещения, по часовой стрелке; расположение — на схеме листа и на листе 85; размеры — в мм по чистовым поверхностям; отметки — в м от ±0,000; высоты Н — от чистого пола помещения до оси изделия, у декора — до центра.
2. Красная цепочка — привязки электроточек и выводов по осям от угла чистовых стен; высота Н — у знака, от чистого пола до оси; высоты мебели, проёмов и границ отделки — колонкой отметок слева. Стена с 5 и более точками или с мелкими звеньями привязок показана двумя видами: архитектурная развёртка (мебель, отделка, проёмы, высоты) и вид «Привязки» на отдельном листе — точки и выводы с марками, одна цепочка по осям и таблица привязок (каждая точка — строка).
3. Стена Б показана двумя видами: здесь — архитектурная развёртка (мебель, отделка, проёмы, высоты), электроточки и выводы ВК с привязками и таблицей — на листе 116 («Привязки»).
4. У знака электроточки: марка (Р — розетка, S — выключатель, Св — светильник, ЭВ — вывод кабеля), ×N — число постов в рамке, гр. — группа щита, Н — высота оси от чистого пола, мм; группы по клавишам выключателя — на листе выключателей.
5. Схема мебели, приборов и декора не является технической документацией для производства мебели; габариты — по паспортам изделий (* — высота не задана в проекте, показана по типовому изделию).
6. Облицовка — по сетке швов 2 мм, раскладка от оси стены (треугольник у пола), по высоте — от середины облицовки, подрезки у пола и у потолка поровну; подрезки — по листу раскладки плитки.
7. Гидроизоляция в 2 слоя, заход на стены 200 мм; над ванной — до 2000 и 300 мм за борт — до облицовки, с актом скрытых работ и тестом проливом (узел — на листе узлов).
8. Картины и зеркала крепить к основанию по паспорту изделия (закладные и анкеры — в перечне скрытых работ); крест — ось центра предмета.
9. Двери скрытого монтажа — полотно в плоскости стены, отделка стены по полотну, плинтус прерывается у короба (узел — на листе узлов).

1000 мм · печать 1:1

Ведомость отделки (на листе)

Марка	Поверхность	Материал, изделие	Цвет, код	Кол.
О10	стены	облицовка плиткой, Atlas Concorde Marvel Travertine, 600×1200×9 мм, A8UZ, затирка CG2WA	Atlas Concorde A8UZ «Marvel Travertine»	13,3 м²
О11	потолок	окраска, Tikkurila Luja 7, матовая, подготовка Q3	Tikkurila V503 «Winter»	8,4 м²

Изм.	Кол.уч	Лист	№ док.	Подп.	Дата
Разраб.		Кырлан А.С.			04.11.26
Пров.					
ГИП					
Н. контр.					
Утв.					

ГД-2026-008-АИ

Квартира с кабинетом

Общая площадь 127,29* м² · * размеры со скана, не замерены (реестр — л. 6–8, К-1)

Дизайн-проект интерьера	Стадия	Лист	Листов
	РП	115	131

Развёртки стен А, Б. Ванная (пом. 7)

М 1:25

Кырлан Александр Сергеевич

выпуск 04.11.2026 № 4177cbe7a3 · стр. 124 из 166

Привязки электроточек и выводов ВК, стена Б. Ванная (пом. 7)

Ванная (пом. 7) · вид изнутри помещения · привязки в мм, отметки в м · к развёртке на листе 115

ПРЕДВАРИТЕЛЬНО · не для производства работ · открыто пунктов: 13 (реестр — л. 6–8)

Развёртка стены Б: электроточки и выводы

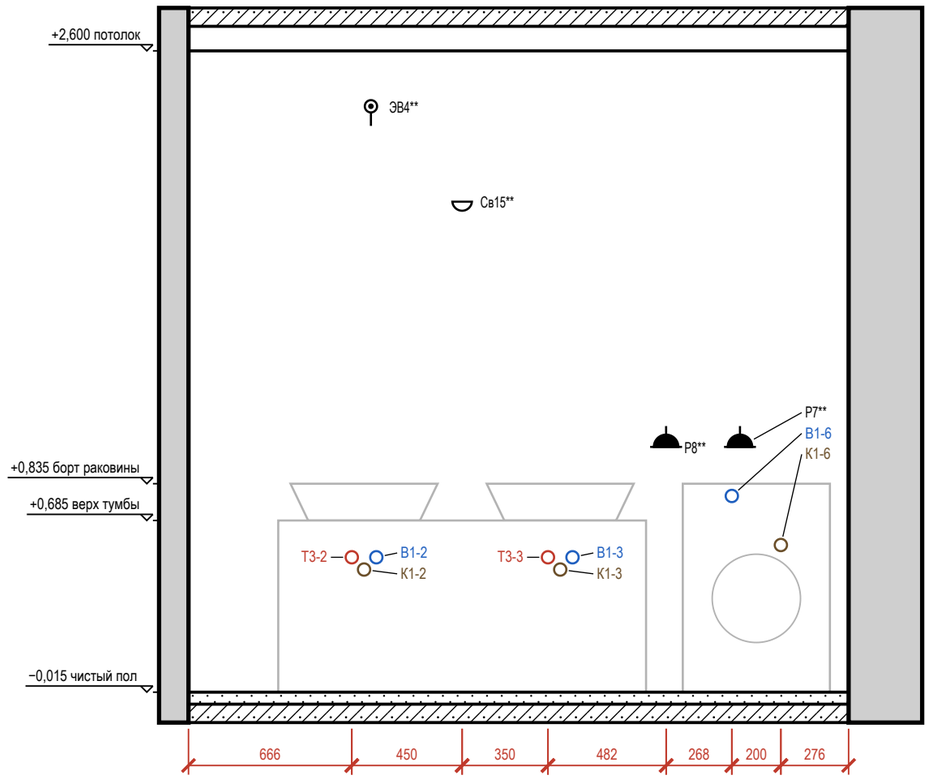


Таблица привязок электроточек и выводов

Марка	Назначение	От угла, мм	Н от пола, мм	Примечание
Т3-2	горячая вода — умывальник	666	550	межос. 100
К1-2	канализация — умывальник	716	500	Ø50
ЭВ4**	вывод кабеля: вентилятор ВР1 (таймер выбега)	744	2389	гр. 3
В1-2	холодная вода — умывальник	766	550	межос. 100
Св15**	светильник настенный	1116	2000	гр. 3
Т3-3	горячая вода — умывальник	1466	550	межос. 100
К1-3	канализация — умывальник	1516	500	Ø50
В1-3	холодная вода — умывальник	1566	550	межос. 100
Р8**	розетка: фен у умывальника	1948	1000	гр. 13, IP44
В1-6	холодная вода — стиральная машина	2216	800	кран машины
Р7**	розетка: стиральная машина	2249	1000	гр. 12, IP44
К1-6	канализация — стиральная машина	2416	600	Ø50

Условные обозначения

- розетка влагозащищённая IP44
- вывод кабеля для подключения прибора (без розетки), марка ЭВ
- светильник настенный (бра), Н — высота оси
- вывод В1 (код — в ведомости привязок)
- вывод Т3 (код — в ведомости привязок)
- вывод К1 (код — в ведомости привязок)
- привязки точек и выводов от угла и от пола, мм

Примечания

1. Вид «Привязки» стены Б — электроточки и выводы ВК; архитектурная развёртка (мебель, отделка, проёмы, высоты) — на листе 115, расположение — на листе 85. Мебель и приборы — подложкой для ориентира; их марки и обозначения мебели, проёмов и стен — там же.
2. Привязки — в мм: по горизонтали от левого чистового угла стены до оси изделия, Н — от чистого пола до оси; все точки — в таблице привязок. Красная цепочка — привязки по осям; точки ближе 150 мм одна к другой в цепочку не дробятся — их привязки только в таблице.
3. У знака — марка электроточки (Р — розетка, S — выключатель, Св — светильник, ЭВ — вывод кабеля); посты в рамке и группа щита — в графе «Примечание»; группы по клавишам выключателя — на листе выключателей.
4. Коды выводов ВК: В1 — холодная вода, Т3 — горячая вода, К1 — канализация; номер после дефиса — номер вывода на листе выводов сантехники.

Допущения и предложения на листе

Основа листа: размеры сняты с растрового плана заказчика с частичными размерами: рисунок не в масштабе, помещения выровнены по подписанным размерам мебели и проходов; контрольный обмер не выполнен (К-1); высота потолка 2700 мм принята: на плане заказчика её нет (К-2); толщины стен 300 / 120 мм приняты по плану заказчика, не замерены (К-1); разрешённая мощность 15 кВт принята по типовым ТУ для квартиры, ТУ заказчиком не переданы (К-4); подрайон климата не задан — принят не северный (жилые от 2,5 м) (К-6). Знак «**» — предложение проектировщика, заказчиком не утверждено (согласовать с заказчиком): Р7 — Сдвиг под раскладку плитки стены Б на 67 мм вдоль стены — ось на шве или в центре плитки, привязка по таблице листа; Р8 — Розетка фена у умывальника на 1000 мм — верхний предел ПУЭ, п. 6.6.30, IP44, как Р7 и Р33; сдвиг под раскладку плитки стены Б на 82 мм вдоль стены — ось на шве или в центре плитки, привязка по таблице листа; Св15 — свет у зеркала — над зеркалом у умывальника по его оси (свет на лицо, а не над сантехникой); ЭВ4 — Вывод вентилятора ВР1 по образцу: группа 3, включение с основным светом, таймер выбега в вентиляторе; сдвиг под раскладку плитки стены Б на 28 мм вдоль стены — ось на шве или в центре плитки, привязка по таблице листа; ИЗ-2, К-5: дверь пом. 7 (стена А) — Проём сдвинут вдоль стены А от угла Б: offset 2300 → 1200 — утверждено автором (ИЗ-2, Кырлан А.С.).

См. лист открытых вопросов (лист 6, записи К-1, К-2, К-4–К-6; лист 7, запись ИЗ-2).

1000 мм · печать 1:1

Изм.	Кол.уч	Лист	№ док.	Подп.	Дата
Разраб.		Кырлан А.С.			04.11.26
Пров.					
ГИП					
Н. контр.					
Утв.					

ГД-2026-008-АИ

Квартира с кабинетом

Общая площадь 127,29* м² · * размеры со скана, не замерены (реестр — л. 6–8, К-1)

Дизайн-проект интерьера

Стадия	Лист	Листов
РП	116	131

Привязки электроточек и выводов ВК, стена Б. Ванная (пом. 7)

М 1:25

Кырлан Александр Сергеевич


выпуск 04.11.2026 · № 4177cbe7a3 · стр. 125 из 166

Развёртки стен В, Г. Ванная (пом. 7)

Ванная (пом. 7) · вид изнутри помещения · размеры в мм, отметки в м


ПРЕДВАРИТЕЛЬНО · не для производства работ · открыто пунктов: 13 (реестр — л. 6–8)

Развёртка стены В

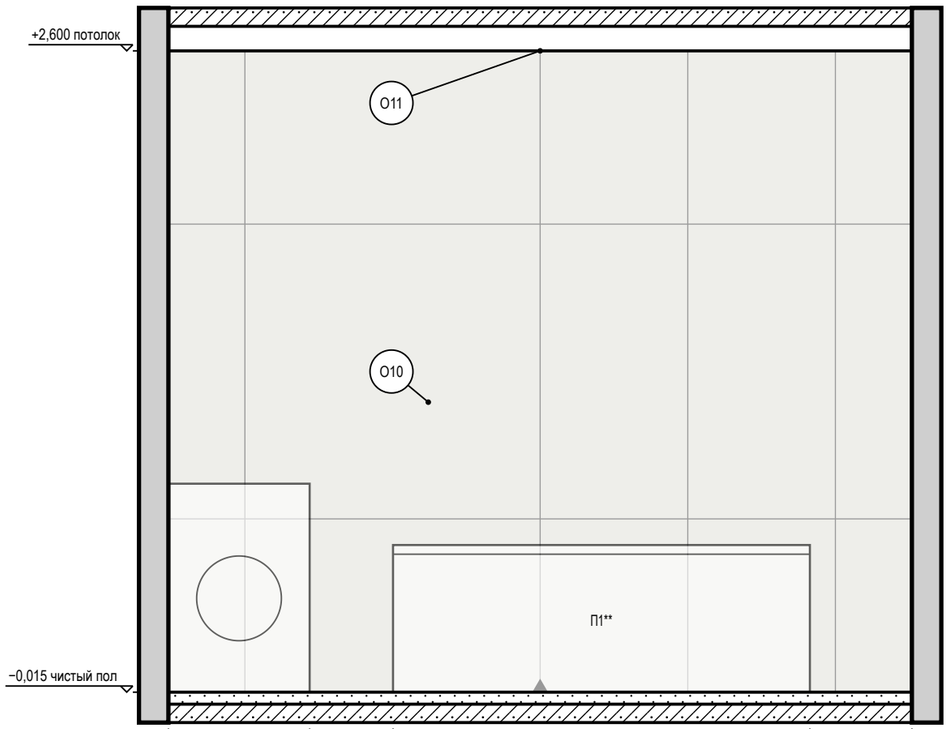


между чистовыми гранями: черновой 3080 − отделка 24 / 24

Развёртка стены Г

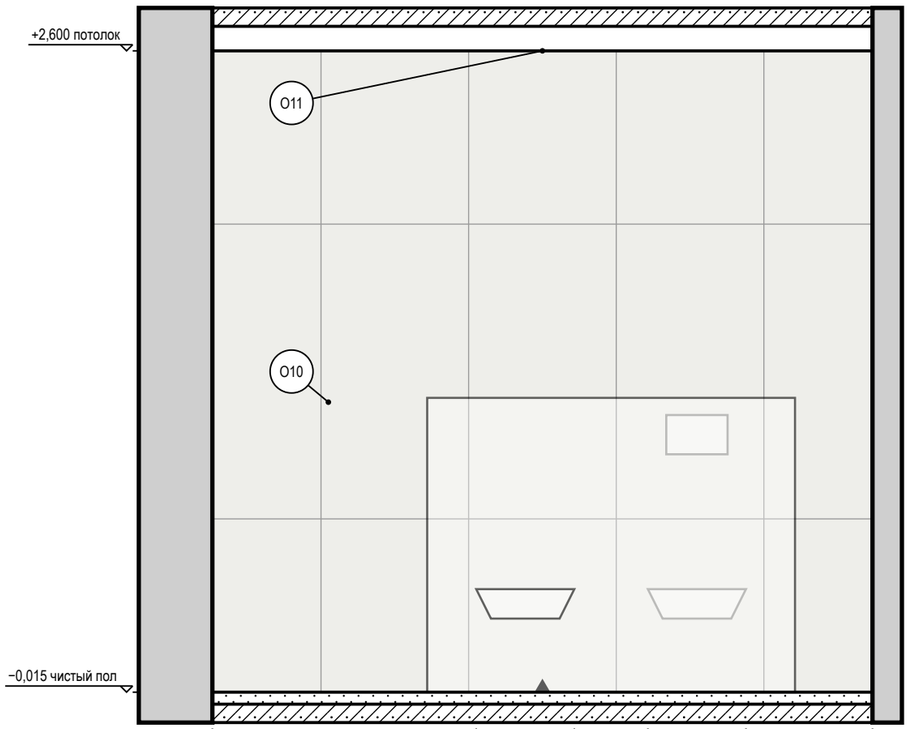

между чистовыми гранями: черновой 2740 − отделка 24 / 24

Схема развёрток (М 1:100)

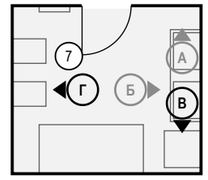

Условные обозначения

- мебель и приборы — фасад по расстановке (условно)
- стены и перекрытия в сечении
- плитка: сетка швов по формату, ▲ — ось старта
- О1 — марка отделки по реестру отделки альбома
- А — марка развёртки: буква стены, стрелка — взгляд

Ведомость отделки (на листе)

Марка	Поверхность	Материал, изделие	Цвет, код	Кол.
О10	стены	облицовка плиткой, Atlas Concorde Marvel Travertine, 600×1200×9 мм, A8UZ, затирка CG2WA	Atlas Concorde A8UZ «Marvel Travertine»	15 м²
О11	потолок	окраска, Tikkurila Luja 7, матовая, подготовка Q3	Tikkurila V503 «Winter»	8,4 м²

Допущения и предложения на листе

Основа листа: размеры сняты с растрового плана заказчика с частичными размерами: рисунок не в масштабе, помещения выровнены по подписанным размерам мебели и проходов; контрольный обмер не выполнен (К-1); высота потолка 2700 мм принята: на плане заказчика её нет (К-2); толщины стен 300 / 120 мм приняты по плану заказчика, не замерены (К-1); разрешённая мощность 15 кВт принята по типовым ТУ для квартиры, ТУ заказчиком не переданы (К-4); подрайон климата не задан — принят не северный (жилые от 2,5 м) (К-6).
Знак «**» — предложение проектировщика, заказчиком не утверждено (согласовать с заказчиком): ИЗ-2, К-5: дверь пом. 7 (стена А) — Проём сдвинут вдоль стены А от угла Б: offset 2300 → 1200 — утверждено автором (ИЗ-2, Кырлан А.С.); К-11: П1 — Стойка смесителя и выводы ванны в полу — предложение проектировщика; пирог пола — К-11.
См. лист открытых вопросов (лист 6, записи К-1, К-2, К-4–К-6, К-11; лист 7, запись ИЗ-2).

Примечания

1. Развёртки — вид на стену изнутри помещения, по часовой стрелке; расположение — на схеме листа и на листе 85; размеры — в мм по чистовым поверхностям; отметки — в м от ±0,000; высоты Н — от чистого пола помещения до оси изделия, у декора — до центра.
2. Стена Г показана двумя видами: здесь — архитектурная развёртка (мебель, отделка, проёмы, высоты), электроточки и выводы ВК с привязками и таблицей — на листе 118 («Привязки»).
3. Схема мебели, приборов и декора не является технической документацией для производства мебели; габариты — по паспортам изделий (* — высота не задана в проекте, показана по типовому изделию).
4. Облицовка — по сетке швов 2 мм, раскладка от оси стены (треугольник у пола), по высоте — от середины облицовки, подрезки у пола и у потолка поровну; подрезки — по листу раскладки плитки.
5. Гидроизоляция в 2 слоя, заход на стены 200 мм; над ванной — до 2000 и 300 мм за борт — до облицовки, с актом скрытых работ и тестом проливом (узел — на листе узлов).

1000 мм · печать 1:1

Изм.	Кол.уч	Лист	№ док.	Подп.	Дата
Разраб.		Кырлан А.С.			04.11.26
Пров.					
ГИП					
Н. контр.					
Утв.					

ГД-2026-008-АИ

Квартира с кабинетом

Общая площадь 127,29* м² · * размеры со скана, не замерены (реестр — л. 6–8, К-1)

Дизайн-проект интерьера	Стадия	Лист	Листов
	РП	117	131

Развёртки стен В, Г. Ванная (пом. 7)

М 1:25

Кырлан Александр Сергеевич

выпуск 04.11.2026 № 4177cbe7a3 · стр. 126 из 166

Привязки выводов ВК, стена Г. Ванная (пом. 7)

Ванная (пом. 7) · вид изнутри помещения · привязки в мм, отметки в м · к развёртке на листе 117

ПРЕДВАРИТЕЛЬНО · не для производства работ · открыто пунктов: 13 (реестр — л. 6–8)

Развёртка стены Г: электроточки и выводы

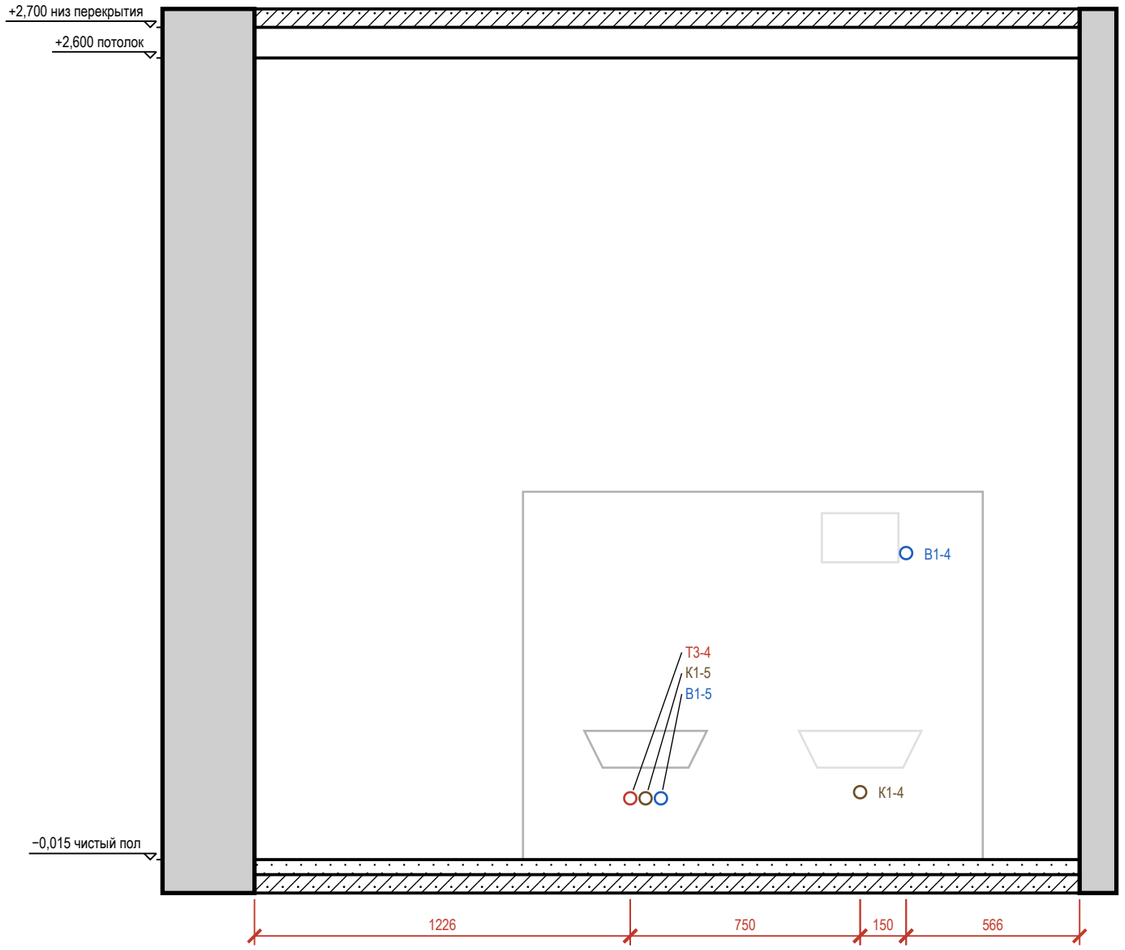



Таблица привязок электроточек и выводов

Марка	Назначение	От угла, мм	H от пола, мм	Примечание
Т3-4	горячая вода — биде подвесное	1226	200	межос. 100, в раме
К1-5	канализация — биде подвесное	1276	200	Ø50
В1-5	холодная вода — биде подвесное	1326	200	межос. 100, в раме
К1-4	канализация — унитаз подвесной	1976	220	Ø110
В1-4	холодная вода — унитаз подвесной	2126	1000	в раме инсталляции

Условные обозначения

- вывод В1 (код — в ведомости привязок)
- вывод Т3 (код — в ведомости привязок)
- вывод К1 (код — в ведомости привязок)
- привязки точек и выводов от угла и от пола, мм
- марка развёртки: буква стены, стрелка — взгляд

Схема развёрток (М 1:50)

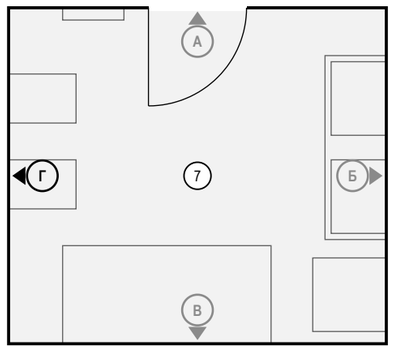

Примечания

1. Вид «Привязки» стены Г — электроточки и выводы ВК; архитектурная развёртка (мебель, отделка, проёмы, высоты) — на листе 117, расположение — на листе 85. Мебель и приборы — подложкой для ориентира; их марки и обозначения мебели, проёмов и стен — там же.
2. Привязки — в мм: по горизонтали от левого чистового угла стены до оси изделия, H — от чистого пола до оси; все точки — в таблице привязок. Красная цепочка — привязки по осям; точки ближе 120 мм одна к другой в цепочку не дробятся — их привязки только в таблице.
3. Коды выводов ВК: В1 — холодная вода, Т3 — горячая вода, К1 — канализация; номер после дефиса — номер вывода на листе выводов сантехники.

Допущения и предложения на листе

Основа листа: размеры сняты с растрового плана заказчика с частичными размерами: рисунок не в масштабе, помещения выровнены по подписанным размерам мебели и проходов; контрольный обмер не выполнен (К-1); высота потолка 2700 мм принята: на плане заказчика её нет (К-2); толщины стен 300 / 120 мм приняты по плану заказчика, не замерены (К-1); разрешённая мощность 15 кВт принята по типовым ТУ для квартиры, ТУ заказчиком не переданы (К-4); подрайон климата не задан — принят не северный (жилые от 2,5 м) (К-6). Знак «**» — предложение проектировщика, заказчиком не утверждено (согласовать с заказчиком): ИЗ-2, К-5: дверь пом. 7 (стена А) — Проём сдвинут вдоль стены А от угла Б: offset 2300 → 1200 — утверждено автором (ИЗ-2, Кырлан А.С.).
См. лист открытых вопросов (лист 6, записи К-1, К-2, К-4–К-6; лист 7, запись ИЗ-2).

1000 мм · печать 1:1

Изм.	Кол.уч	Лист	№ док.	Подп.	Дата
Разраб.		Кырлан А.С.			04.11.26
Пров.					
ГИП					
Н. контр.					
Утв.					

ГД-2026-008-АИ

Квартира с кабинетом

Общая площадь 127,29* м² · * размеры со скана, не замерены (реестр — л. 6–8, К-1)

	Стадия	Лист	Листов
Дизайн-проект интерьера	РП	118	131

Привязки выводов ВК, стена Г. Ванная (пом. 7)

М 1:20

Кырлан Александр Сергеевич


выпуск 04.11.2026 № 4177cbe7a3 · стр. 127 из 166

Развёртка стены Б. Прихожая (пом. 8)

Прихожая (пом. 8) · вид изнутри помещения · размеры в мм, отметки в м

ПРЕДВАРИТЕЛЬНО · не для производства работ · открыто пунктов: 13 (реестр — л. 6–8)

Развёртка стены Б

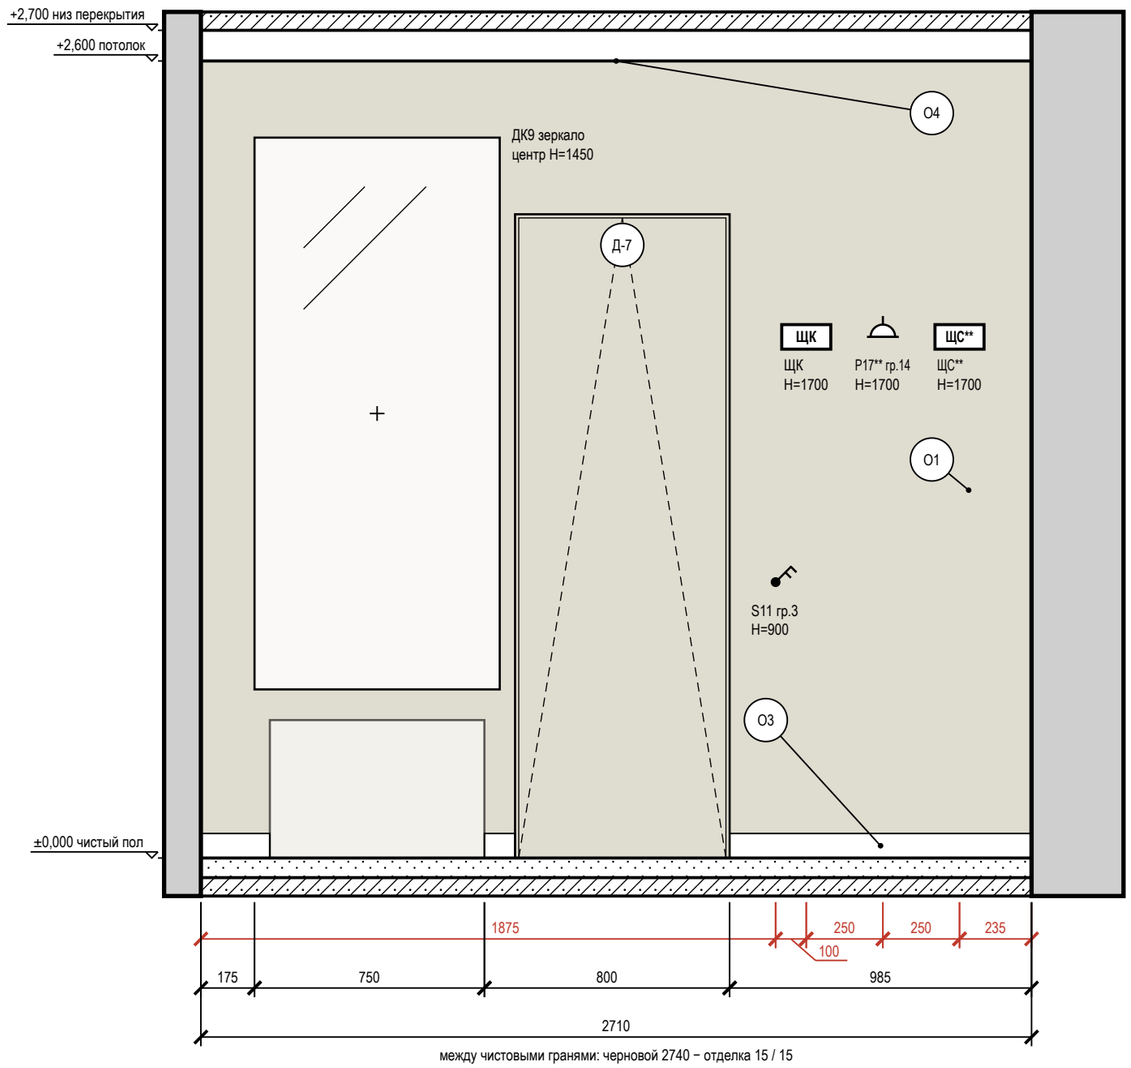

между чистовыми гранями: черновой 2740 − отделка 15 / 15

Допущения и предложения на листе

Основа листа: размеры сняты с растрового плана заказчика с частичными размерами: рисунок не в масштабе, помещения выровнены по подписанным размерам мебели и проходов; контрольный обмер не выполнен (К-1); высота потолка 2700 мм принята: на плане заказчика её нет (К-2); толщины стен 300 / 120 мм приняты по плану заказчика, не замерены (К-1); разрешённая мощность 15 кВт принята по типовым ТУ для квартиры, ТУ заказчиком не переданы (К-4); подрайон климата не задан — принят не северный (жилые от 2,5 м) (К-6).

Знак «**» — предложение проектировщика, заказчиком не утверждено (согласовать с заказчиком): Р17 — высота 1700 мм выше нормы 1 м (ПУЭ 6.6.30) по назначению: питание слаботочного щита ЩС, рядом со щитом на его высоте; ЩС — щит слаботочный: место и состав.


См. лист открытых вопросов (лист 6, записи К-1, К-2, К-4, К-6).

Примечания

1. Развёртки — вид на стену изнутри помещения, по часовой стрелке; расположение — на схеме листа и на листе 85; размеры — в мм по чистовым поверхностям; отметки — в м от ±0,000; высоты Н — от чистого пола помещения до оси изделия, у декора — до центра.
2. Красная цепочка — привязки электроточек и выводов по осям от угла чистовых стен; высота Н — у знака, от чистого пола до оси; высоты мебели, проёмов и границ отделки — колонкой отметок слева. Стена с 5 и более точками или с мелкими звеньями привязок показана двумя видами: архитектурная развёртка (мебель, отделка, проёмы, высоты) и вид «Привязки» на отдельном листе — точки и выводы с марками, одна цепочка по осям и таблица привязок (каждая точка — строка).
3. У знака электроточки: марка (Р — розетка, S — выключатель, Св — светильник, ЭВ — вывод кабеля), ×N — число постов в рамке, гр. — группа щита, Н — высота оси от чистого пола, мм; группы по клавишам выключателя — на листе выключателей.
4. Схема мебели, приборов и декора не является технической документацией для производства мебели; габариты — по паспортам изделий.
5. Картины и зеркала крепить к основанию по паспорту изделия (закладные и анкеры — в перечне скрытых работ); крест — ось центра предмета.
6. Двери скрытого монтажа — полотно в плоскости стены, отделка стены по полотну, плинтус прерывается у короба (узел — на листе узлов).

1000 мм · печать 1:1

Схема развёрток (М 1:100)

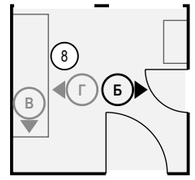

Условные обозначения

- розетка с заземляющим контактом; у знака — марка, ×N постов в рамке, гр. — группа щита, Н — высота оси, мм
- выключатель одноклавишный
- выключатель двухклавишный (флажков — по числу клавиш)
- ЩК — щит квартирный
- привязки точек и выводов от угла и от пола, мм
- мебель и приборы — фасад по расстановке (условно)
- зеркало: марка Д, крест — центр, Н — высота центра, мм
- дверь скрытого монтажа: полотно в плоскости стены (узел — на листе узлов)
- стены и перекрытия в сечении
- окраска: тон — цвет по коду производителя (условно)
- О1 — марка отделки по реестру отделки альбома
- А — марка развёртки: буква стены, стрелка — взгляд

Ведомость отделки (на листе)

Марка	Поверхность	Материал, изделие	Цвет, код	Кол.
О1	стены	окраска, Farrow & Ball Modern Emulsion, матовая, подготовка Q3	Farrow & Ball No. 15 «Bone — мягкий каменно-серый с зеленцой»	5,6 м²
О3	плинтус	плинтус МДФ, h 80 мм, аналог: плинтус МДФ под покраску 80×16	Farrow & Ball No. 15 «Bone — мягкий каменно-серый с зеленцой»	1,3 м
О4	потолок	окраска, Tikkurila Anti-Reflex 2, глубокоматовая, подготовка Q3	Tikkurila V503 «Winter»	7,9 м²

Изм.	Кол.уч	Лист	№ док.	Подп.	Дата
Разраб.		Кырлан А.С.			04.11.26
Пров.					
ГИП					
Н. контр.					
Утв.					

ГД-2026-008-АИ

Квартира с кабинетом

Общая площадь 127,29* м² · * размеры со скана, не замерены (реестр — л. 6–8, К-1)

Дизайн-проект интерьера

Стадия	Лист	Листов
РП	119	131

Развёртка стены Б. Прихожая (пом. 8)

М 1:20

Кырлан Александр Сергеевич


выпуск 04.11.2026 № 4177cbe7a3 · стр. 128 из 166

Развёртки стен В, Г. Прихожая (пом. 8)

Прихожая (пом. 8) · вид изнутри помещения · размеры в мм, отметки в м


ПРЕДВАРИТЕЛЬНО · не для производства работ · открыто пунктов: 13 (реестр — л. 6–8)

Развёртка стены В

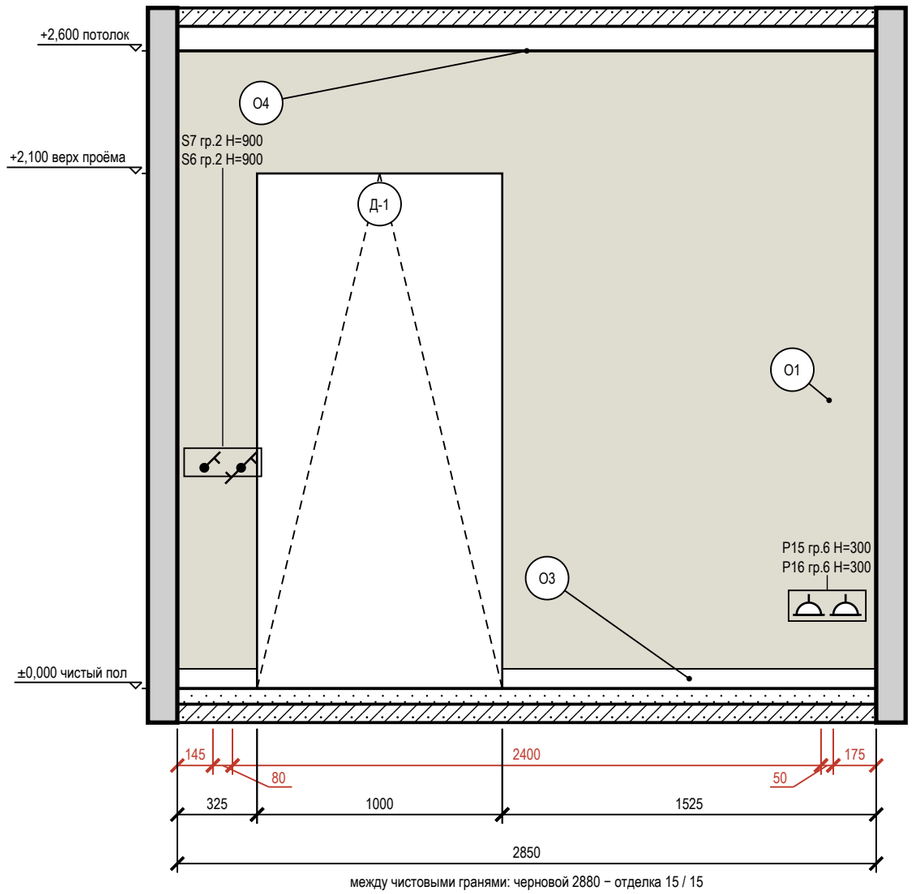


между чистовыми гранями: черновой 2880 − отделка 15 / 15

Развёртка стены Г

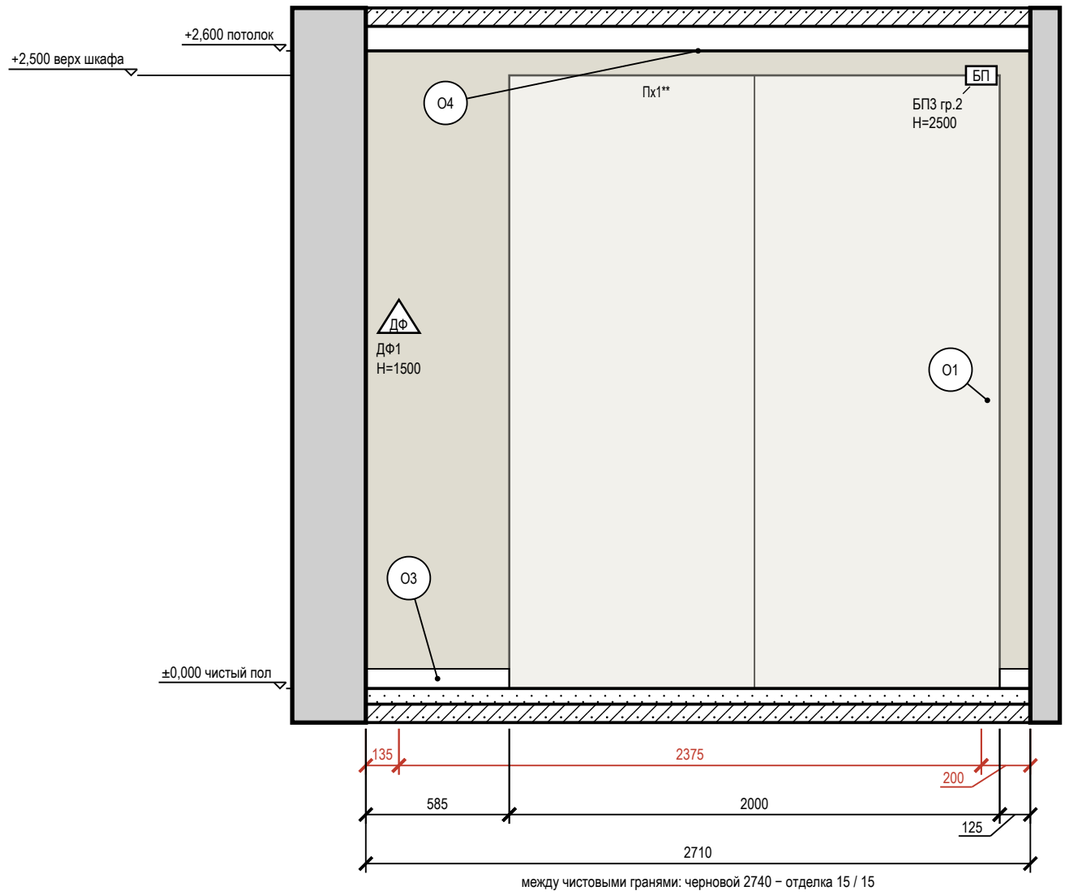

между чистовыми гранями: черновой 2740 − отделка 15 / 15

Схема развёрток (М 1:100)

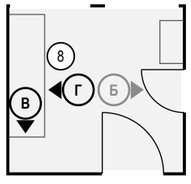

Условные обозначения

- розетка с заземляющим контактом; у знака — марка, ×N постов в рамке, гр. — группа щита, H — высота оси, мм
- выключатель одноклавишный
- выключатель с проходной или перекрёстной клавишей (обратный флажок); тип клавиши — в подписи
- БП — блок питания LED, с доступом (люк от 100×100 мм)
- ДФ — трубка или монитор домофона
- привязки точек и выводов от угла и от пола, мм
- мебель и приборы — фасад по расстановке (условно)
- дверной проём; марка двери — в кружке
- стены и перекрытия в сечении
- окраска: тон — цвет по коду производителя (условно)
- О1 — марка отделки по реестру отделки альбома
- А — марка развёртки: буква стены, стрелка — взгляд

Допущения и предложения на листе

Основа листа: размеры сняты с растрового плана заказчика с частичными размерами: рисунок не в масштабе, помещения выровнены по подписанным размерам мебели и проходов; контрольный обмер не выполнен (К-1); высота потолка 2700 мм принята: на плане заказчика её нет (К-2); толщины стен 300 / 120 мм приняты по плану заказчика, не замерены (К-1); разрешённая мощность 15 кВт принята по типовым ТУ для квартиры, ТУ заказчиком не переданы (К-4); подрайон климата не задан — принят не северный (жилые от 2,5 м) (К-6).
Знак «**» — предложение проектировщика, заказчиком не утверждено (согласовать с заказчиком): ИЗ-1: Пх1 — фасад купе по кадру визуализации прихожей: МДФ 10 мм, эмаль матовая, латунный профиль, зеркальные арочные вставки (поле 100 мм).
См. лист открытых вопросов (лист 6, записи К-1, К-2, К-4, К-6; лист 7, запись ИЗ-1).

Примечания

1. Развёртки — вид на стену изнутри помещения, по часовой стрелке; расположение — на схеме листа и на листе 85; размеры — в мм по чистовым поверхностям; отметки — в м от ±0,000; высоты H — от чистого пола помещения до оси изделия, у декора — до центра.
2. Красная цепочка — привязки электроточек и выводов по осям от угла чистовых стен; высота H — у знака, от чистого пола до оси; высоты мебели, проёмов и границ отделки — колонкой отметок слева. Стена с 5 и более точками или с мелкими звеньями привязок показана двумя видами: архитектурная развёртка (мебель, отделка, проёмы, высоты) и вид «Привязки» на отдельном листе — точки и выводы с марками, одна цепочка по осям и таблица привязок (каждая точка — строка).
3. У знака электроточки: марка (Р — розетка, S — выключатель, Св — светильник, ЭВ — вывод кабеля), ×N — число постов в рамке, гр. — группа щита, H — высота оси от чистого пола, мм; группы по клавишам выключателя — на листе выключателей.
4. Схема мебели, приборов и декора не является технической документацией для производства мебели; габариты — по паспортам изделий.

1000 мм · печать 1:1

Изм.	Кол.уч	Лист	№ док.	Подп.	Дата
Разраб.		Кырлан А.С.			04.11.26
Пров.					
ГИП					
Н. контр.					
Утв.					

ГД-2026-008-АИ

Квартира с кабинетом

Общая площадь 127,29* м² · * размеры со скана, не замерены (реестр — л. 6–8, К-1)

Дизайн-проект интерьера

Стадия	Лист	Листов
РП	120	131

Развёртки стен В, Г. Прихожая (пом. 8)

М 1:25

Кырлан Александр Сергеевич


выпуск 04.11.2026 № 4177cbe7a3 · стр. 129 из 166

Развёртки стен А, Б, В. Санузел гостевой (пом. 9)

Санузел гостевой (пом. 9) · вид изнутри помещения · размеры в мм, отметки в м


ПРЕДВАРИТЕЛЬНО · не для производства работ · открыто пунктов: 13 (реестр — л. 6–8)

Развёртка стены А

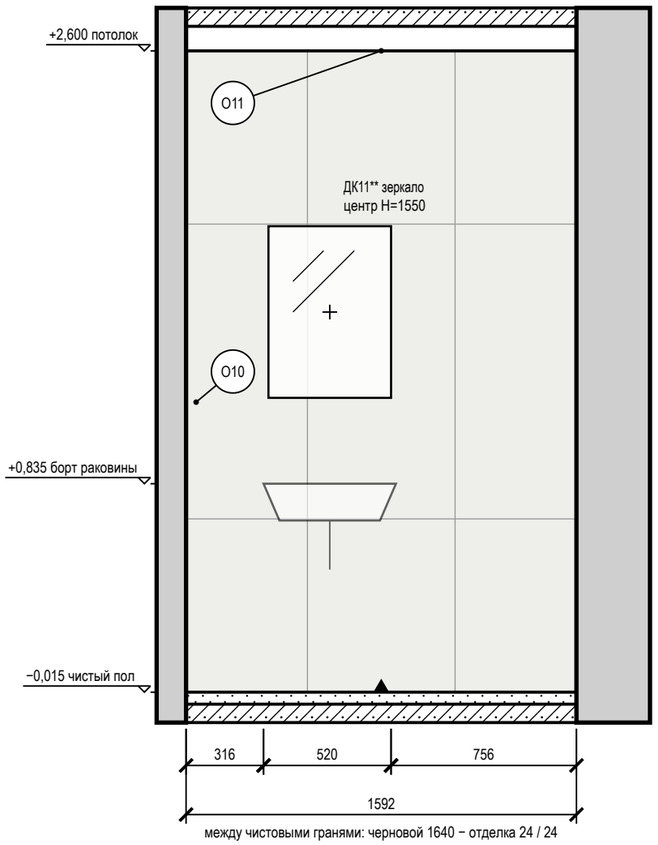


между чистовыми гранями: черновой 1640 − отделка 24 / 24

Развёртка стены Б

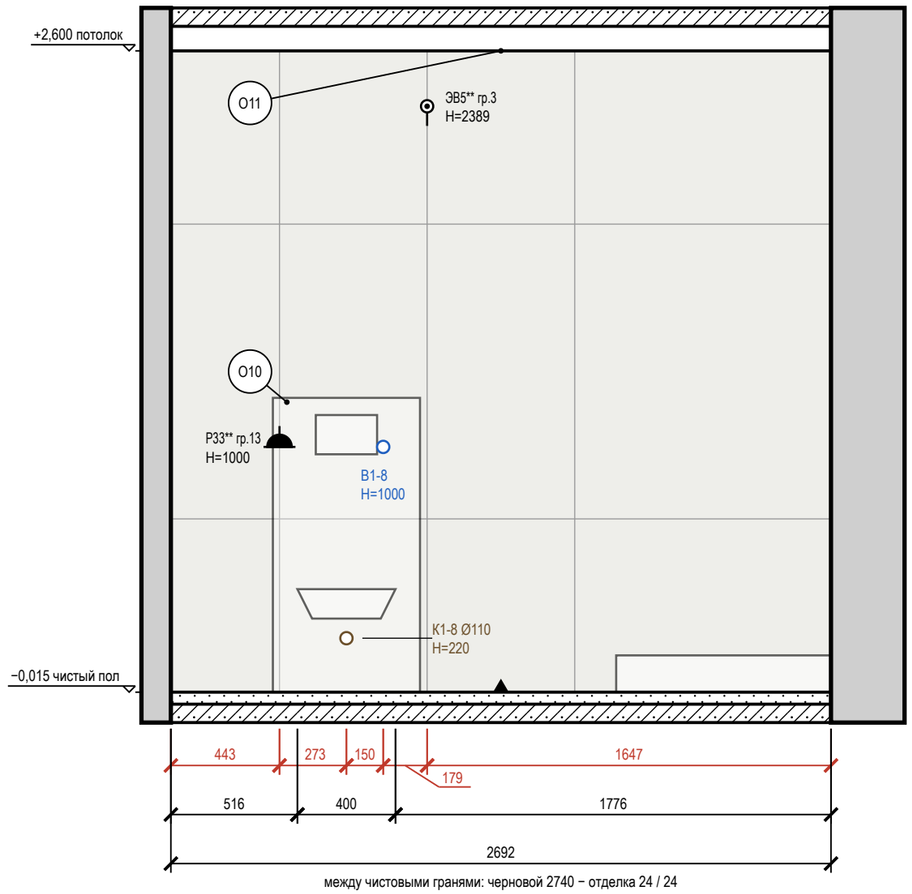


между чистовыми гранями: черновой 2740 − отделка 24 / 24

Развёртка стены В

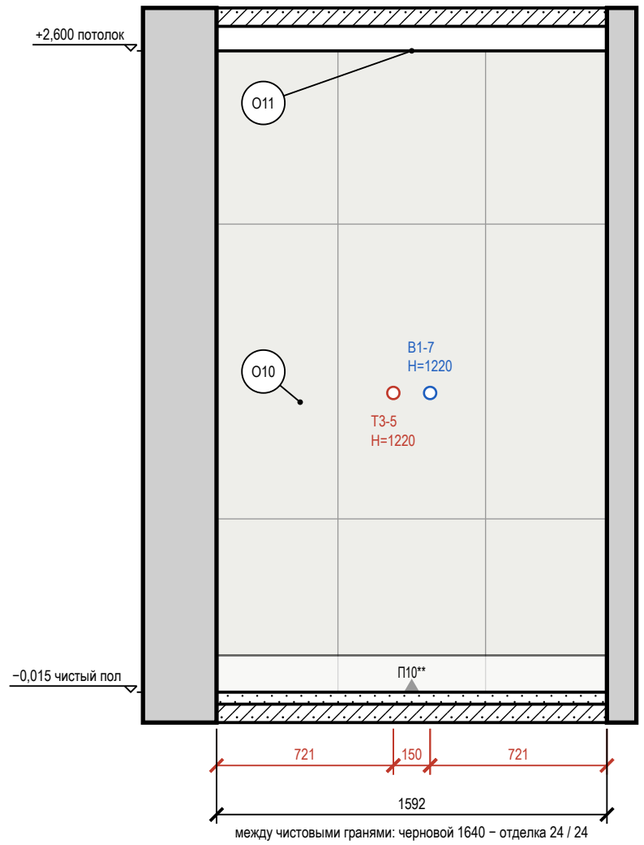

между чистовыми гранями: черновой 1640 − отделка 24 / 24

Схема развёрток (М 1:100)

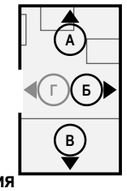

Условные обозначения

- розетка влагозащищённая IP44
- вывод кабеля для подключения прибора (без розетки), марка ЭВ
- вывод В1 (код — в ведомости привязок)
- вывод Т3 (код — в ведомости привязок)
- вывод К1 (код — в ведомости привязок)
- привязки точек и выводов от угла и от пола, мм
- мебель и приборы — фасад по расстановке (условно)
- зеркало: марка Д, крест — центр, Н — высота центра, мм
- стены и перекрытия в сечении
- плитка: сетка швов по формату, ▲ — ось старта
- О1 — марка отделки по реестру отделки альбома
- А — марка развёртки: буква стены, стрелка — взгляд

Ведомость отделки (на листе)

Марка	Поверхность	Материал, изделие	Цвет, код	Кол.
О10	стены	облицовка плиткой, Atlas Concorde Marvel Travertine, 600×1200×9 мм, A8UZ, затирка CG2WA	Atlas Concorde A8UZ «Marvel Travertine»	15,4 м²
О11	потолок	окраска, Tikkurila Luja 7, матовая, подготовка Q3	Tikkurila V503 «Winter»	4,5 м²

Примечания

1. Развёртки — вид на стену изнутри помещения, по часовой стрелке; расположение — на схеме листа и на листе 85; размеры — в мм по чистовым поверхностям; отметки — в м от ±0,000; высоты Н — от чистого пола помещения до оси изделия, у декора — до центра.
2. Красная цепочка — привязки электроточек и выводов по осям от угла чистовых стен; высота Н — у знака, от чистого пола до оси; высоты мебели, проёмов и границ отделки — колонкой отметок слева. Стена с 5 и более точками или с мелкими звеньями привязок показана двумя видами: архитектурная развёртка (мебель, отделка, проёмы, высоты) и вид «Привязки» на отдельном листе — точки и выводы с марками, одна цепочка по осям и таблица привязок (каждая точка — строка).
3. Стена А показана двумя видами: здесь — архитектурная развёртка (мебель, отделка, проёмы, высоты), электроточки и выводы ВК с привязками и таблицей — на листе 122 («Привязки»).
4. У знака электроточки: марка (Р — розетка, S — выключатель, Св — светильник, ЭВ — вывод кабеля), ×N — число постов в рамке, гр. — группа щита, Н — высота оси от чистого пола, мм; группы по клавишам выключателя — на листе выключателей.
5. Схема мебели, приборов и декора не является технической документацией для производства мебели; габариты — по паспортам изделий (* — высота не задана в проекте, показана по типовому изделию).
6. Облицовка — по сетке швов 2 мм, раскладка от оси стены (треугольник у пола), по высоте — от середины облицовки, подрезки у пола и у потолка поровну; подрезки — по листу раскладки плитки.
7. Гидроизоляция в 2 слоя, заход на стены 200 мм; у душа — на всю высоту стен душевой зоны и 500 мм за край душевой зоны — до облицовки, с актом скрытых работ и тестом проливом (узел — на листе узлов).
8. Картины и зеркала крепить к основанию по паспорту изделия (закладные и анкеры — в перечне скрытых работ); крест — ось центра предмета.

1000 мм · печать 1:1

Допущения и предложения на листе. Знак «**» предложено (согласовать). См. лист открытых вопросов (листы 6–8).

Изм.	Кол.уч	Лист	№ док.	Подп.	Дата			
Разраб.		Кырлан А.С.			04.11.26	ГД-2026-008-АИ		
Пров.						Квартира с кабинетом Общая площадь 127,29* м² · * размеры со скана, не замерены (реестр — л. 6–8, К-1)		
ГИП						Дизайн-проект интерьера	Стадия: РП	Лист: 121 / Листов: 131
Н. контр.						Развёртки стен А, Б, В. Санузел гостевой (пом. 9) М 1:25	Кырлан Александр Сергеевич	
Утв.								

выпуск 04.11.2026 № 4177cbe7a3 · стр. 130 из 166

Привязки электроточек и выводов ВК, стена А. Санузел гостевой (пом. 9)

Санузел гостевой (пом. 9) · вид изнутри помещения · привязки в мм, отметки в м · к развёртке на листе 121

ПРЕДВАРИТЕЛЬНО · не для производства работ · открыто пунктов: 13 (реестр — л. 6–8)

Развёртка стены А: электроточки и выводы

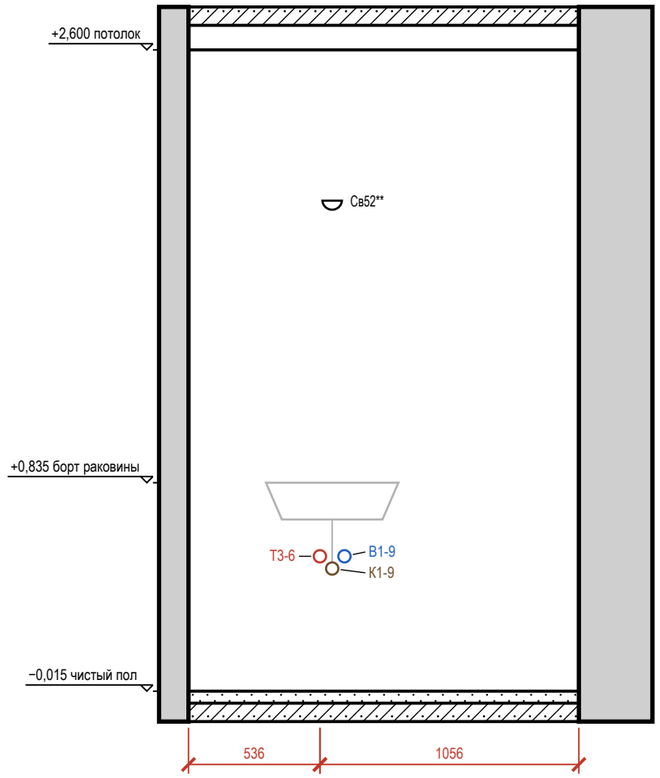



Таблица привязок электроточек и выводов

Марка	Назначение	От угла, мм	Н от пола, мм	Примечание
Т3-6	горячая вода — умывальник	536	550	межос. 100
К1-9	канализация — умывальник	586	500	Ø50
Св52**	светильник настенный	586	2000	гр. 3
В1-9	холодная вода — умывальник	636	550	межос. 100

Условные обозначения

- светильник настенный (бра), Н — высота оси
- вывод В1 (код — в ведомости привязок)
- вывод Т3 (код — в ведомости привязок)
- вывод К1 (код — в ведомости привязок)
- привязки точек и выводов от угла и от пола, мм
- марка развёртки: буква стены, стрелка — взгляд

Схема развёрток (М 1:50)

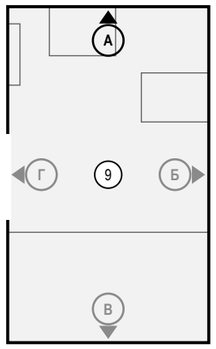

Примечания

1. Вид «Привязки» стены А — электроточки и выводы ВК; архитектурная развёртка (мебель, отделка, проёмы, высоты) — на листе 121, расположение — на листе 85. Мебель и приборы — подложкой для ориентира; их марки и обозначения мебели, проёмов и стен — там же.
2. Привязки — в мм: по горизонтали от левого чистового угла стены до оси изделия, Н — от чистого пола до оси; все точки — в таблице привязок. Красная цепочка — привязки по осям; точки ближе 150 мм одна к другой в цепочку не дробятся — их привязки только в таблице.
3. У знака — марка электроточки (Р — розетка, S — выключатель, Св — светильник, ЭВ — вывод кабеля); посты в рамке и группа щита — в графе «Примечание»; группы по клавишам выключателя — на листе выключателей.
4. Коды выводов ВК: В1 — холодная вода, Т3 — горячая вода, К1 — канализация; номер после дефиса — номер вывода на листе выводов сантехники.

Допущения и предложения на листе

Основа листа: размеры сняты с растрового плана заказчика с частичными размерами: рисунок не в масштабе, помещения выровнены по подписанным размерам мебели и проходов; контрольный обмер не выполнен (К-1); высота потолка 2700 мм принята: на плане заказчика её нет (К-2); толщины стен 300 / 120 мм приняты по плану заказчика, не замерены (К-1); разрешённая мощность 15 кВт принята по типовым ТУ для квартиры, ТУ заказчиком не переданы (К-4); подрайон климата не задан — принят не северный (жилые от 2,5 м) (К-6). Знак «**» — предложение проектировщика, заказчиком не утверждено (согласовать с заказчиком): Св52 — свет у зеркала — над зеркалом у умывальника по его оси (свет на лицо, а не над сантехникой).

См. лист открытых вопросов (лист 6, записи К-1, К-2, К-4, К-6).

1000 мм · печать 1:1

Изм.	Кол.уч	Лист	№ док.	Подп.	Дата
Разраб.		Кырлан А.С.			04.11.26
Пров.					
ГИП					
Н. контр.					
Утв.					

ГД-2026-008-АИ

Квартира с кабинетом

Общая площадь 127,29* м² · * размеры со скана, не замерены (реестр — л. 6–8, К-1)

Дизайн-проект интерьера	Стадия	Лист	Листов
	РП	122	131

Привязки электроточек и выводов ВК, стена А. Санузел гостевой (пом. 9)

М 1:25

Кырлан Александр Сергеевич

выпуск 04.11.2026 № 4177cbe7a3 · стр. 131 из 166

Развёртка стены Г. Санузел гостевой (пом. 9)

Санузел гостевой (пом. 9) · вид изнутри помещения · размеры в мм, отметки в м

ПРЕДВАРИТЕЛЬНО · не для производства работ · открыто пунктов: 13 (реестр — л. 6–8)

Развёртка стены Г


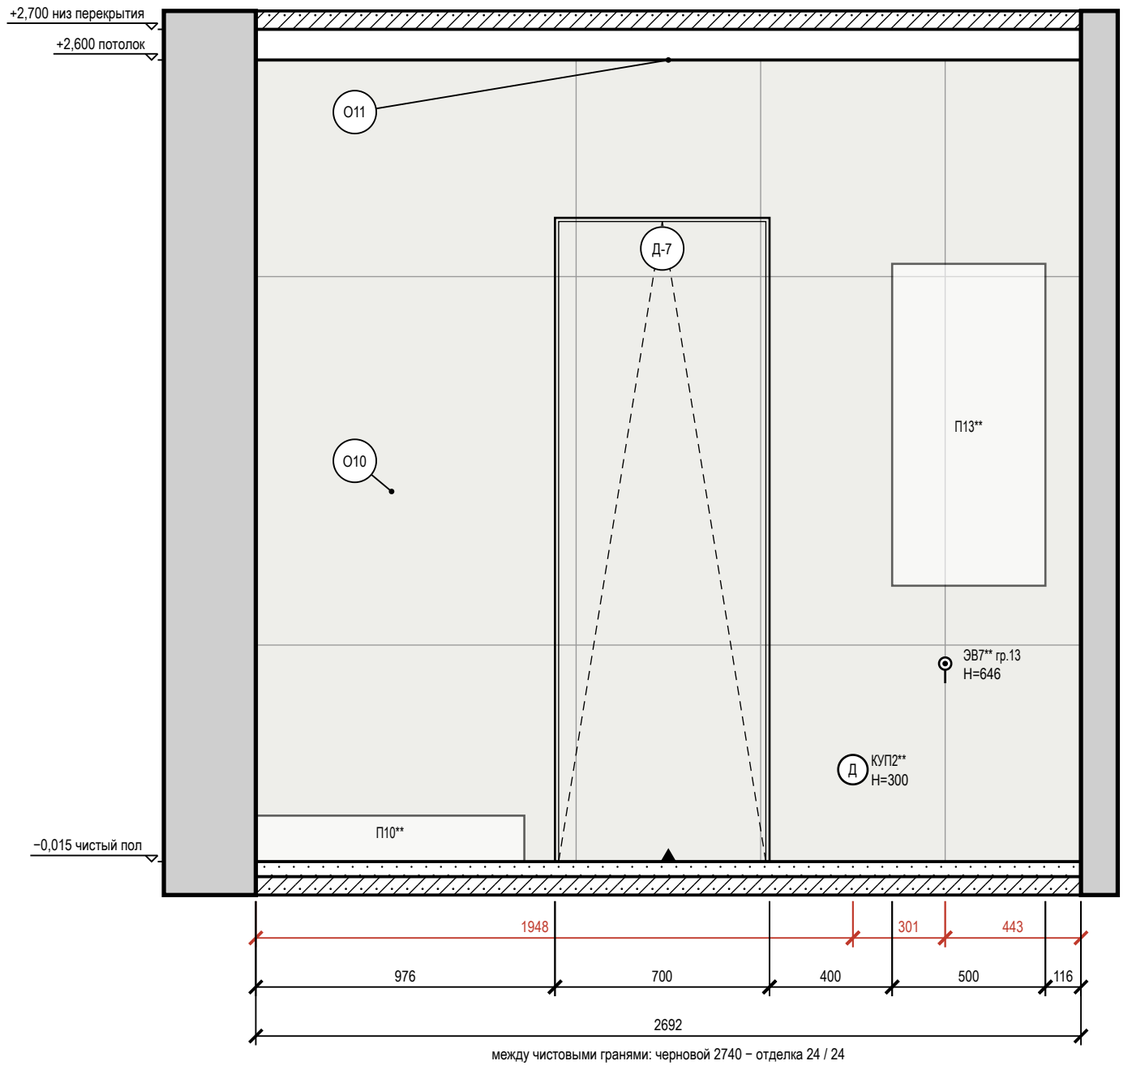


Схема развёрток (М 1:100)

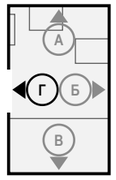

Условные обозначения

- вывод кабеля для подключения прибора (без розетки), марка ЭВ
- привязки точек и выводов от угла и от пола, мм
- мебель и приборы — фасад по расстановке (условно)
- дверь скрытого монтажа: полотно в плоскости стены (узел — на листе узлов)
- стены и перекрытия в сечении
- плитка: сетка швов по формату, ▲ — ось старта
- О1 — марка отделки по реестру отделки альбома
- А — марка развёртки: буква стены, стрелка — взгляд

Ведомость отделки (на листе)

Марка	Поверхность	Материал, изделие	Цвет, код	Кол.
О10	стены	облицовка плиткой, Atlas Concorde Marvel Travertine, 600×1200×9 мм, A8UZ, затирка CG2WA	Atlas Concorde A8UZ «Marvel Travertine»	5,6 м²
О11	потолок	окраска, Tikkurila Luja 7, матовая, подготовка Q3	Tikkurila V503 «Winter»	4,5 м²

Допущения и предложения на листе. Основа листа: размеры сняты с растрового плана заказчика с частичными размерами: рисунок не в масштабе, помещения выровнены по подписанным размерам мебели и проходов; контрольный обмер не выполнен (К-1); высота потолка 2700 мм принята: на плане заказчика её нет (К-2); толщины стен 300 / 120 мм приняты по плану заказчика, не замерены (К-1); разрешённая мощность 15 кВт принята по типовым ТУ для квартиры, ТУ заказчиком не переданы (К-4); подрайон климата не задан — принят не северный (жилые от 2,5 м) (К-6). Знак «**» — предложено, не утверждено (согласовать): П13, КУП2, ЭВ7; К-10: П10. См. лист открытых вопросов (лист 6, записи К-1, К-2, К-4, К-6, К-10).

Примечания

1. Развёртки — вид на стену изнутри помещения, по часовой стрелке; расположение — на схеме листа и на листе 85; размеры — в мм по чистовым поверхностям; отметки — в м от ±0,000; высоты Н — от чистого пола помещения до оси изделия, у декора — до центра.
2. Красная цепочка — привязки электроточек и выводов по осям от угла чистовых стен; высота Н — у знака, от чистого пола до оси; высоты мебели, проёмов и границ отделки — колонкой отметок слева. Стена с 5 и более точками или с мелкими звеньями привязок показана двумя видами: архитектурная развёртка (мебель, отделка, проёмы, высоты) и вид «Привязки» на отдельном листе — точки и выводы с марками, одна цепочка по осям и таблица привязок (каждая точка — строка).
3. У знака электроточки: марка (Р — розетка, S — выключатель, Св — светильник, ЭВ — вывод кабеля), ×N — число постов в рамке, гр. — группа щита, Н — высота оси от чистого пола, мм; группы по клавишам выключателя — на листе выключателей.
4. Схема мебели, приборов и декора не является технической документацией для производства мебели; габариты — по паспортам изделий (* — высота не задана в проекте, показана по типовому изделию).
5. Облицовка — по сетке швов 2 мм, раскладка от оси стены (треугольник у пола), по высоте — от середины облицовки, подрезки у пола и у потолка поровну; подрезки — по листу раскладки плитки.
6. Гидроизоляция в 2 слоя, заход на стены 200 мм; у душа — на всю высоту стен душевой зоны и 500 мм за край душевой зоны — до облицовки, с актом скрытых работ и тестом проливом (узел — на листе узлов).
7. Двери скрытого монтажа — полотно в плоскости стены, отделка стены по полотну, плинтус прерывается у короба (узел — на листе узлов).

1000 мм · печать 1:1

Изм.	Кол.уч	Лист	№ док.	Подп.	Дата
Разраб.		Кырлан А.С.			04.11.26
Пров.					
ГИП					
Н. контр.					
Утв.					

ГД-2026-008-АИ

Квартира с кабинетом

Общая площадь 127,29* м² · * размеры со скана, не замерены (реестр — л. 6–8, К-1)

Дизайн-проект интерьера

Стадия	Лист	Листов
РП	123	131

Развёртка стены Г. Санузел гостевой (пом. 9)

М 1:20

Кырлан Александр Сергеевич


выпуск 04.11.2026 № 4177cbe7a3 · стр. 132 из 166

Узлы

Пороги и стыки покрытий, скрытые двери, короба стояков, гидроизоляция, плинтус


1 Порог 15 мм: мокрая зона — смежное помещение (М 1:10)

Применение: двери Д-6, Д-7; места — лист 85

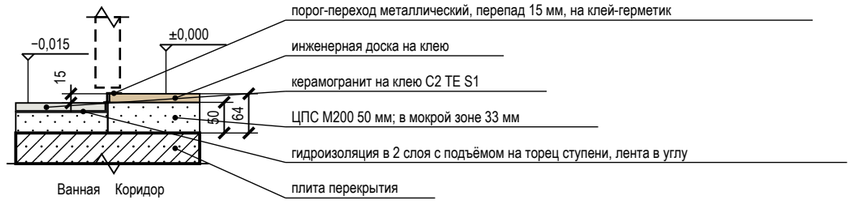


2 Дверь скрытого монтажа в плоскости стены, плинтус (М 1:5)

Применение: двери Д-2, Д-3, Д-4, Д-5, Д-6, Д-7; места — лист 85

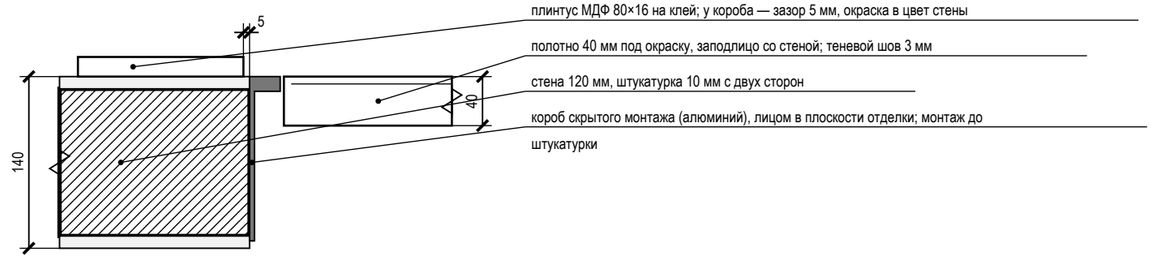


3 Короб стояков К1-1 с люком и звукоизоляцией (М 1:10)

Применение: пом. 9, 7, 4; места — лист 85

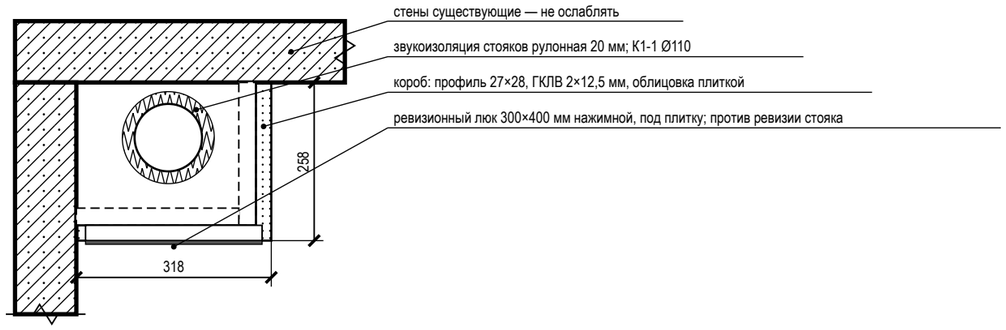

4 Гидроизоляция санузла: заход на стены 200 мм (М 1:20)

Применение: пом. 7, 9; места — лист 85

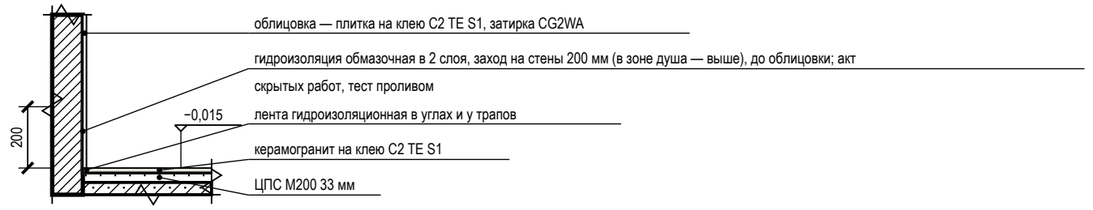


Допущения и предложения на листе

Основа листа: размеры сняты с растрового плана заказчика с частичными размерами: рисунок не в масштабе, помещения выровнены по подписанным размерам мебели и проходов; контрольный обмер не выполнен (К-1); высота потолка 2700 мм принята: на плане заказчика её нет (К-2); толщины стен 300 / 120 мм приняты по плану заказчика, не замерены (К-1); разрешённая мощность 15 кВт принята по типовым ТУ для квартиры, ТУ заказчиком не переданы (К-4); подрайон климата не задан — принят не северный (жилые от 2,5 м) (К-6).
См. лист открытых вопросов (лист 6, записи К-1, К-2, К-4, К-6).


5 Плинтус МДФ 80×16 мм у окрашенной стены по доске (ламинату) (М 1:10)

Применение: пом. 1, 2, 3, 4, 5, 6; места — лист 85

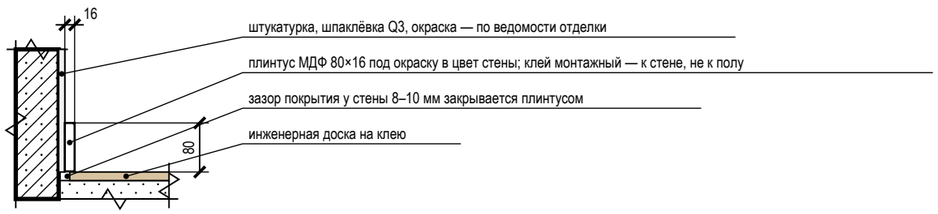

6 Плинтус МДФ 80×16 мм у окрашенной стены по керамограниту (плитке) (М 1:10)

Применение: пом. 8; места — лист 85

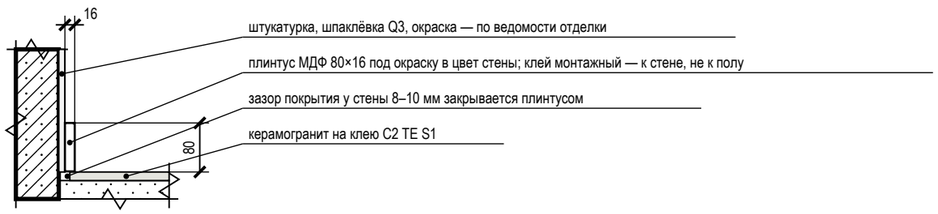

Условные обозначения

- железобетон (плита, стены) — условно: конструкция не установлена
- кладка, перегородка — условно: конструкция не установлена
- стяжка, раствор
- гипсокартон ГКЛВ
- звукоизоляция, эластичный заполнитель
- плитка, керамогранит на клею
- инженерная доска (покрытие пола)
- металлический профиль (порог, Т-профиль, короб двери)
- гидроизоляция (обмазочная, лента)

Примечания

1. Узлы — типовые решения проекта для мест, отмеченных выносками на листе схемы расположения развёрток и узлов; размеры — в мм, отметки — в м от ±0,000.
2. Узлы с гидроизоляцией, закладными и коробами скрытого монтажа принимаются по актам скрытых работ до закрытия отделкой; гидроизоляция — после теста проливом (24 ч).
3. Марки изделий (порог, Т-профиль, короб скрытой двери, люк) — по спецификациям; замена — на аналог с теми же габаритами по согласованию с автором проекта.
4. Материал плиты перекрытия и стен в узлах показан условно (железобетон, кладка): конструкция дома не установлена — крепёж, анкеры и толщины слоёв уточняются после обследования (до него — по допущениям общих указаний).

Изм.	Кол.уч	Лист	№ док.	Подп.	Дата
Разраб.		Кырлан А.С.			04.11.26
Пров.					
ГИП					
Н. контр.					
Утв.					

ГД-2026-008-АИ

Квартира с кабинетом

Общая площадь 127,29* м² · * размеры со скана, не замерены (реестр — л. 6–8, К-1)

Дизайн-проект интерьера

Стадия	Лист	Листов
РП	124	131

Узлы

М 1:10; 1:5; 1:20

Кырлан Александр Сергеевич

выпуск 04.11.2026 № 4177cbe7a3 · стр. 133 из 166

10

Смета

Кырлан Александр Сергеевич

выпуск 04.11.2026 № 4177cbe7a3 · стр. 134 из 166

Ведомость объёмов работ

ПРЕДВАРИТЕЛЬНО · не для производства работ · открыто пунктов: 13 (реестр — л. 6–8)

Объёмы по помещениям от чертежа · площади в м², длины в м · формула, правило проёмов и источник в каждой строке

Ведомость объёмов работ по помещениям

Поз.	Наименование работ (материал, число слоёв)	Ед. изм.	Объём по помещениям (№ по экспликации)									Всего	Формула подсчёта	Правило проёмов	Источник	Цена за ед., ₽	Стоимость, ₽
			1	2	3	4	5	6	7	8	9						
1. Демонтаж и черновые работы																	
1	Демонтаж существующего покрытия пола до основания	м²	17,89	5,11	18,92	45,51	9,07	9,97	8,44	7,89	4,49	127,29	S пом.		л. 15, 16	по КП	
2	Демонтаж существующей отделки стен до основания	м²	35,92	22,94	38,05	62,33	31,82	25,90	28,76	20,40	21,44	287,56	P × H − проёмы	за вычетом проёмов	л. 15, 16	по КП	
3	Демонтаж существующей отделки потолка до основания	м²	17,89	5,11	18,92	45,51	9,07	9,97	8,44	7,89	4,49	127,29	S пом.		л. 15, 16	по КП	
4	Демонтаж существующих дверных блоков	шт	1	1	1			1	1	2		7	по ведомости проёмов		л. 16–18	по КП	
5	Демонтаж существующих сантехприборов и электрооборудования (если есть)	компл											по факту на объекте		л. 16	по КП	
6	Устройство стяжки: стяжка ЦПС М200, 50 мм	м²	17,94	5,15	18,97	45,58	9,39	10,02	8,49	8,23	4,53	128,30	S пом. + S в дверных проёмах (b × t/2)	проёмы добавлены	л. 58–60	530	67 999
7	Гидроизоляция обмазочная, 2 слоя: пол, стены на 200 мм, зоны замачивания	м²							14,64		15,38	30,02	пол + (P − двери) × h заведения + зоны замачивания		л. 54	450	13 509
8	Штукатурка стен по маякам, до 10 мм	м²	35,92	22,94	38,05	62,33	31,82	25,90	28,76	20,40	21,44	287,56	P × H − проёмы по обводу коробок − грани перегородок на ГКЛВ	за вычетом проёмов	л. 15, 59, 60	530	152 407
9	Штукатурка оконных откосов шириной более 200 мм	м²	2,16		2,07	2,94		2,09				9,26	Σ (2h + b) × глубина откоса	откосы > 200 мм	л. 15	540	5 000
10	Потолок ГКЛ по каркасу П113, 1 слой	м²	17,89		18,92	45,51	9,07	9,97	8,44	7,89	4,49	122,18	S пом. по плану потолков		л. 48–53	1 500	183 270
Итого по разделу 1 — 422 185 ₽ (позиций 10, из них по КП 5); в сводную смету — л. 130, 131																	
2. Инженерные системы																	
11	Прокладка кабеля ВВГнг(A)-LS по группам щита: за потолком и в штробах стен (штробы — только после технического заключения, см. строку «Штробы в стенах»)	м										521,70	Σ длин групп щита		л. 30, 31	60	31 302
12	Прокладка слаботочной линии: Кабель домофона — тип по системе поставщика, отдельно от силовых	м										5,70	по лучам от ЩС**: 1 точ., запас 10 %		л. 33	по КП	
13	Прокладка слаботочной линии: Кабель коаксиальный RG-6 (75 Ом) к розеткам ТВ, отдельно от силовых	м										57,00	по лучам от ЩС**: 3 точ., запас 10 %		л. 33	по КП	
14	Прокладка слаботочной линии: Кабель U/UTP кат. 6 (LAN, Wi-Fi и камеры по PoE), отдельно от силовых	м										110,60	по лучам от ЩС**: 7 точ., запас 10 %		л. 33	по КП	
15	Прокладка гофротрубы Ø20 для слаботочных линий, отдельно от силовых	м										156,00	по длине лучей без участков в канале плинтуса (≈ 90 %)		л. 33	по КП	
16	Сборка слаботочного щита ЩС**: корпус, патч-панель, подключение линий и питания 220 В; коммутатор и точки доступа — оборудование заказчика	шт										1	один щит		л. 28, 29, 33	по КП	
17	Электроточка: подрозетник в бетоне, розетка, выключатель, вывод	шт	11		10	22	4	8	4	8	3	70	по ведомости электроточек		л. 25, 28, 29	950	66 500
18	Штробы в стенах под спуски кабеля к точкам — выполняются только после технического заключения о несущих стенах	м	18,35		14,00	28,79	7,40	16,00	5,37	11,70	3,81	105,42	Σ (H − h) по точкам на стенах: вертикальные спуски	после техзаключения	л. 16, 25	по КП	
19	Установка встраиваемого точечного светильника	шт	8		6	16	2	6	3	4	2	47	по плану освещения		л. 26	750	35 250
20	Монтаж светильника: потолочного, подвесного, настенного	шт	2	1	2	3		2	1		1	12	по плану освещения		л. 26	1 200	14 400
21	Монтаж LED-ленты в алюминиевый профиль	м	13,30		14,30	7,70		9,60		1,80		46,70	Σ длин лент по плану освещения		л. 26	230	10 741
22	Установка блока питания LED в доступном месте (люк, шкаф)	шт	1		1	1		1		1		5	один на LED-группу		л. 26	570	2 850
23	Установка автономного пожарного извещателя	шт	1		1	2	1	1		1		7	по плану розеток		л. 25	по КП	

Допущения и предложения на листе

Основа листа: размеры сняты с растрового плана заказчика с частичными размерами: рисунок не в масштабе, помещения выровнены по подписанным размерам мебели и проходов; контрольный обмер не выполнен (К-1); высота потолка 2700 мм принята: на плане заказчика её нет (К-2); толщины стен 300 / 120 мм приняты по плану заказчика, не замерены (К-1); разрешённая мощность 15 кВт принята по типовым ТУ для квартиры, ТУ заказчиком не переданы (К-4); подрайон климата не задан — принят не северный (жилые от 2,5 м) (К-6).
Знак «**» — предложение проектировщика, заказчиком не утверждено (согласовать с заказчиком): ЩС — щит слаботочный: место и состав.
См. лист открытых вопросов (лист 6, записи К-1, К-2, К-4, К-6).

Изм.	Кол.уч	Лист	№ док.	Подп.	Дата
Разраб.		Кырлан А.С.			04.11.26
Пров.					
ГИП					
Н. контр.					
Утв.					

ГД-2026-008-АИ

Квартира с кабинетом

Общая площадь 127,29* м² · * размеры со скана, не замерены (реестр — л. 6–8, К-1)

Дизайн-проект интерьера

Стадия	Лист	Листов
РП	125	131

Ведомость объёмов работ

М б/м

Кырлан Александр Сергеевич

Ведомость объёмов работ (продолжение)

ПРЕДВАРИТЕЛЬНО · не для производства работ · открыто пунктов: 13 (реестр — л. 6–8)

Объёмы по помещениям от чертежа · площади в м², длины в м · формула, правило проёмов и источник в каждой строке

Ведомость объёмов работ по помещениям (продолжение)

Поз.	Наименование работ (материал, число слоёв)	Ед. изм.	Объём по помещениям (№ по экспликации)									Всего	Формула подсчёта	Правило проёмов	Источник	Цена за ед., ₽	Стоимость, ₽
			1	2	3	4	5	6	7	8	9						
24	Сборка щита: установка автоматов и АВДТ групп, вводного автомата	шт										15	группы + вводной автомат		л. 30, 31	230	3 450
25	Установка вводного УЗО	шт										1	по однолинейной схеме		л. 30, 31	380	380
26	Монтаж инсталляции, установка подвесного унитаза и кнопки смыва	шт							2		1	3	по плану выводов		л. 36, 46	10 500	31 500
27	Короб инсталляции: каркас и обшивка ГКЛВ в 2 слоя, ревизионный доступ к смыву	шт							2		1	3	по плану выводов		л. 36, 54–57	по КП	
28	Короб К1 над чистым полом: каркас и обшивка ГКЛВ под плитку (материалы — в спецификации ВК)	м.п.							7,72		2,42	10,14	Σ открытых участков выпусков К1 (профиль листа разводки ВК)		л. 36, 46	по КП	
29	Установка ванны с сифоном	шт							1			1	по плану выводов		л. 36, 46	6 000	6 000
30	Установка умывальника (мойки) с сифоном и смесителем	шт							2		1	3	по плану выводов		л. 36, 46	3 000	9 000
31	Установка душевого поддона с трапом, ограждения	шт									1	1	по плану выводов		л. 36, 46	по КП	
32	Подключение стиральной (посудомоечной) машины к ВК	шт							1			1	по плану выводов		л. 36	по КП	
33	Монтаж островной вытяжки Кх6** к плите перекрытия (закладная, подвес по паспорту модели), подключение к выводу питания; рециркуляция — угольный фильтр в комплекте	шт				1						1	по листам вентиляции и потолков: 1		л. 34, 48–53	по КП	
34	Установка радиатора с узлом подключения и терморегулятором	шт	2		2	3		2				9	по плану отопления		л. 35	по КП	
Итого по разделу 2 — 211 373 ₽ (позиций 24, из них по КП 13); в сводную смету — л. 130, 131																	
3. Чистовые работы																	
35	Облицовка стен керамогранитом 600×1200 на клею	м²							26,96		20,72	47,68	по раскладке: зона облицовки − место за коробом	за вычетом проёмов	л. 54–57	2 500	119 200
36	Облицовка короба инсталляции (ГКЛВ) керамогранитом: лицо, боковины, полка	м²							2,77		1,47	4,24	по раскладке: лицо, боковины, полка		л. 54–57	2 500	10 600
37	Облицовка фартука керамогранитом 1200×600	м²				0,70						0,70	по раскладке фартука		л. 54–57, 59, 60	2 400	1 680
38	Укладка керамогранита на пол, 600×600, на клею	м²							8,49	8,23	4,53	21,25	S пом. + S в дверных проёмах	проёмы добавлены	л. 54–58	1 800	38 250
39	Затирка швов керамогранита	м²				0,70			38,17	7,89	26,68	73,44	Σ S облицовки и пола из плитки		л. 54–57	150	11 016
40	Грунтование стен, 2 слоя (под штукатурку и под отделку)	м²	35,92	22,94	38,05	62,33	31,82	25,90	28,76	20,40	21,44	287,56	P × H − проёмы	за вычетом проёмов	л. 59, 60	96	27 606
41	Шпаклёвка стен под окраску, 2 слоя (старт и финиш), уровень Q3	м²	35,92	22,94	38,05	61,63	31,82	25,90		20,40		236,66	P × H − проёмы − фартук	за вычетом проёмов	л. 59, 60	750	177 495
42	Грунтование и шпаклёвка оконных откосов, 2 слоя	м.п.	9,40		9,00	12,80		9,10				40,30	Σ (2h + b) по окнам	по окнам	л. 15	300	12 090
43	Грунтование потолка, 2 слоя	м²	17,89	5,11	18,92	45,51	9,07	9,97	8,44	7,89	4,49	127,29	S пом.		л. 59, 60	96	12 220
44	Шпаклёвка потолка под окраску, 2 слоя, уровень Q3	м²	17,89	5,11	18,92	45,51	9,07	9,97	8,44	7,89	4,49	127,29	S пом.		л. 48–53, 59, 60	950	120 926
45	Окраска потолка водно-дисперсионной краской, 2 слоя	м²	17,89	5,11	18,92	45,51	9,07	9,97	8,44	7,89	4,49	127,29	S пом.		л. 59, 60	360	45 824
46	Окраска стен водно-дисперсионной краской, 2 слоя	м²	42,40	24,41	44,10	69,71	42,95	31,90		29,22		284,69	P × H − фартук, проёмы не вычитаются	без вычета проёмов	л. 59, 60	300	85 407
47	Окраска оконных откосов, 2 слоя	м.п.	9,40		9,00	12,80		9,10				40,30	Σ (2h + b) по окнам	по окнам	л. 15	120	4 836
48	Укладка инженерной доски на клей	м²	17,94	5,15	18,97	45,58	9,39	10,02				107,05	S пом. + S в дверных проёмах	проёмы добавлены	л. 58–60	1 200	128 460

Допущения и предложения на листе

Основа листа: размеры сняты с растрового плана заказчика с частичными размерами: рисунок не в масштабе, помещения выровнены по подписанным размерам мебели и проходов; контрольный обмер не выполнен (К-1); высота потолка 2700 мм принята: на плане заказчика её нет (К-2); толщины стен 300 / 120 мм приняты по плану заказчика, не замерены (К-1); разрешённая мощность 15 кВт принята по типовым ТУ для квартиры, ТУ заказчиком не переданы (К-4); подрайон климата не задан — принят не северный (жилые от 2,5 м) (К-6).
Знак «**» — предложение проектировщика, заказчиком не утверждено (согласовать с заказчиком): ИЗ-8: Кх6 — Остров сдвинут от кухонного ряда: торец острова стоял в 900 мм от фронта ПММ Кх3 и модуля Кх4 — меньше 1000 мм (СП 31-107-2004, п. 6.1.12) и меньше 1200 мм, при которых открытые ПММ и ящики не перекрывают проход.
См. лист открытых вопросов (лист 6, записи К-1, К-2, К-4, К-6; лист 8, запись ИЗ-8).

Изм.	Кол.уч	Лист	№ док.	Подп.	Дата
Разраб.		Кырлан А.С.			04.11.26
Пров.					
ГИП					
Н. контр.					
Утв.					

ГД-2026-008-АИ

Квартира с кабинетом

Общая площадь 127,29* м² · * размеры со скана, не замерены (реестр — л. 6–8, К-1)

Дизайн-проект интерьера	Стадия	Лист	Листов
	РП	126	131

Ведомость объёмов работ (продолжение)

М б/м

Кырлан Александр Сергеевич

Ведомость объёмов работ (окончание)

ПРЕДВАРИТЕЛЬНО · не для производства работ · открыто пунктов: 13 (реестр — л. 6–8)

Объёмы по помещениям от чертежа · площади в м², длины в м · формула, правило проёмов и источник в каждой строке

Ведомость объёмов работ по помещениям (продолжение)

Поз.	Наименование работ (материал, число слоёв)	Ед. изм.	Объём по помещениям (№ по экспликации)									Всего	Формула подсчёта	Правило проёмов	Источник	Цена за ед., ₽	Стоимость, ₽
			1	2	3	4	5	6	7	8	9						
49	Установка плинтуса МДФ h=80 мм	м.п.	16,16	8,34	16,74	25,88	11,22	11,96		7,04		97,34	P − ширина дверных проёмов		л. 59, 60	450	43 803
50	Окраска плинтуса в тоне No. 15, 2 слоя	м.п.	16,16	8,34	16,74	25,88	11,22	11,96		7,04		97,34	как плинтус		л. 59, 60	300	29 202
51	Монтаж дверей скрытого монтажа под покраску (поставщик дверей)	шт	1	1	1			1	1	1		6	по ведомости проёмов		л. 17, 18	5 250	31 500
52	Входная дверь, поставка с монтажом и откосами	шт										1	по ведомости проёмов		л. 17, 18	по КП	
Итого по разделу 3 — 900 115 ₽ (позиций 18, из них по КП 1); в сводную смету — л. 130, 131																	

Ведомость подсчёта площадей по помещениям

№	Помещение	S пола, м²	P, м	H, м	P × H, м²	Проёмы, м²	Стены нетто, м²	В дверных проёмах, м²	Плинтус, м	Откосы, м.п.
1	Спальня	17,89	16,96	2,50	42,40	6,48	35,92	0,05	16,16	9,40
2	Гардеробная-постирочная	5,11	9,04	2,70	24,41	1,47	22,94	0,04	8,34	нет
3	Кабинет	18,92	17,64	2,50	44,10	6,05	38,05	0,05	16,74	9,00
4	Кухня-гостиная	45,51	27,08	2,60	70,41	8,08	62,33	0,07	25,88	12,80
5	Коридор	9,07	16,52	2,60	42,95	11,13	31,82	0,32	11,22	нет
6	Детская	9,97	12,76	2,50	31,90	6,00	25,90	0,05	11,96	9,10
7	Ванная	8,44	11,64	2,62	30,44	1,68	28,76	0,05	нет	нет
8	Прихожая	7,89	11,24	2,60	29,22	8,82	20,40	0,34	7,04	нет
9	Санузел гостевой	4,49	8,76	2,62	22,91	1,47	21,44	0,04	нет	нет
	Итого	**127,29**			**338,74**	**51,18**	**287,56**	**1,01**	**97,34**	**40,30**

Реестр контрольных сумм

Показатель	По ВОР	По чертежу	Расхождение	Лист
Σ площадей помещений без летних, м² — общая площадь по экспликации	127,29	127,29	0,0 %	л. 15
Стены под окраску, м² (шпаклёвка) ведомость отделки	236,66	236,66	0,0 %	л. 59, 60
Потолки под окраску, м² — ведомость отделки	127,29	127,29	0,0 %	л. 59, 60
Плинтус, м — ведомость отделки	97,34	97,34	0,0 %	л. 59, 60
Плитка к заказу, шт — ведомость плитки	209	209	0,0 %	л. 54
Гидроизоляция, м² — ведомость материалов плитки	30,02	30,02	0,0 %	л. 54
Точки ЭОМ, шт — планы ЭОМ (без щитов)	146	148	-1,4 %	л. 25, 26

Примечания

1. Объёмы — от геометрии проекта (та же, что на планах и в ведомости отделки), не от общей площади: P — периметр чистого контура, H — от чистого пола до низа потолка, проёмы — по наружному обводу коробок.
2. Подсчёт по ГЭСН-2001-15 и ГЭСН-2001-11: штукатурка и шпаклёвка стен — за вычетом проёмов; окраска водными составами — без вычета проёмов (п. 2.24); откосы — отдельно, по ширине до 200 и более 200 мм; полы — с площадью в дверных проёмах.
3. Плитка — по раскладке (целые и с подрезкой); короб инсталляции и фартук — отдельными строками, двойного счёта облицовки нет. Материалы, запас и количество к заказу — в спецификации материалов.
4. Цены — ориентир по открытым прайсам Москвы (цены на 21.09.2026), не коммерческое предложение; «по КП» — расценки нет, строка в итог не входит.
5. Демонтаж — по плану демонтажа и общим указаниям: покрытия пола, отделка стен и потолков, дверные блоки — до основания; объёмы справочные — по плану демонтажа (расценки в книге нет — «по КП»).
6. Штробы в стенах — только после технического заключения о несущих стенах (общие указания, план обмера и демонтажа): строка «Штробы в стенах» вертикальные спуски кабеля от потолочной трассы к точкам, объём не меньше фактического (горизонтальные трассы — по исполнительной схеме). Расценки штробления в прайсе нет — «по КП», в итог не входит; кабель в штробах стен прокладывается после неё.
7. Площадь облицовки стен — одно число с тремя названиями: зона облицовки по ведомости отделки 50,20 м² − место за коробом инсталляции 2,52 м² (плитку туда не кладут) = стены под плитку 47,68 м² (строка «Облицовка стен»); облицовка коробов 4,24 м² — отдельной строкой; стены и короба вместе — 51,92 м² (столько плитки по раскладке в спецификации). Источник — один (quantities.js), расхождение на листах ловит.
8. Слаботочные сети: кабель по лучам от ЩС** 173,30 м (U/UTP, RG-6, домофон — по видам), гофра 156,00 м, щит ЩС** с патч-панелью; розетки RJ45 и ТВ монтируются в строке «Электроточка». Длины те же, что в ведомости изделий электрика (одна модель — lowcurrent-engineer/bom.js); оборудование заказчика (точки доступа, камеры, коммутатор) в спецификацию не входит. 3 точ. — предложение листа слаботочки.
9. Коробы: стояков (нет) и К1 над чистым полом (10,14 м открытых участков; труба К1 вдоль стен 29,58 м в короб не зашивается — она за приборами, в раме инсталляции и в шахтах). В спецификации ВК короб К1 заказывается с запасом 10 % — 11,20 м. Материалы коробов стояков и инсталляции — в спецификации материалов, К1 — в спецификации ВК.

Допущения и предложения на листе

Основа листа: размеры сняты с растрового плана заказчика с частичными размерами: рисунок не в масштабе, помещения выровнены по подписанным размерам мебели и проходов; контрольный обмер не выполнен (К-1); высота потолка 2700 мм принята: на плане заказчика её нет (К-2); толщины стен 300 / 120 мм приняты по плану заказчика, не замерены (К-1); разрешённая мощность 15 кВт принята по типовым ТУ для квартиры, ТУ заказчиком не переданы (К-4); подрайон климата не задан — принят не северный (жилые от 2,5 м) (К-6). Знак «**» — предложение проектировщика, заказчиком не утверждено (согласовать с заказчиком): ЩС — щит слаботочный: место и состав. См. лист открытых вопросов (лист 6, записи К-1, К-2, К-4, К-6).

Изм.	Кол.уч	Лист	№ док.	Подп.	Дата	ГД-2026-008-АИ			
						Квартира с кабинетом			
						Общая площадь 127,29* м² · * размеры со скана, не замерены (реестр — л. 6–8, К-1)			
Разраб.		Кырлан А.С.			04.11.26	Дизайн-проект интерьера	Стадия	Лист	Листов
Пров.							РП	127	131
ГИП									
						Ведомость объёмов работ (окончание)	**Кырлан Александр Сергеевич**		
Н. контр.						М б/м			
Утв.									

выпуск 04.11.2026 № 4177cbe7a3 · стр. 137 из 166

Спецификация материалов

Отделочные материалы: чистое количество, запас, упаковка, к заказу · ГОСТ 21.110-2013

ПРЕДВАРИТЕЛЬНО · не для производства работ · открыто пунктов: 13 (реестр — л. 6–8)

Спецификация материалов (ГОСТ 21.110-2013, форма 1)

Поз.	Наименование и техническая характеристика	Тип, марка, артикул	Код продукции	Поставщик	Ед. изм.	Количество				Масса ед., кг	Примечание
						чистое	запас, %	упаковка	к заказу		
Покрытия полов и облицовка											
1	Инженерная доска (дуб натуральный, рабочий слой 4 мм, эмиссия E1, прямая укладка)	1167-4250			м²	107,05	7	по артикулу	114,60 м²		пом. 1, 2, 3, 4, 5, 6; до целой упаковки; л. 58–60
2	Клей для паркетной и инженерной доски (эластичный, по ТУ изготовителя доски)	по выбору подрядчика			м²	107,05		ведро по ТУ	по ТУ		расход кг/м² — по ТУ клея; л. 58
3	Керамогранит 600×600 мм под травертин	аналог: керамогранит под травертин			шт	46	10	коробка	51 шт		15 целых + 31 с подрезкой; 12,93 м² по раскладке, к заказу 18,36 м²; пом. 7, 9; л. 54–57
4	Керамогранит 600×1200 мм A8UZ	A8UZ			шт	137	10	коробка	155 шт		18 целых + 119 с подрезкой; 59,81 м² по раскладке, к заказу 111,60 м²; пом. 7, 8, 9; л. 54–57
5	Керамогранит 1200×600 мм под травертин, матовый	аналог: керамогранит под травертин, матовый			шт	2	10	коробка	3 шт		0 целых + 2 с подрезкой; 0,70 м² по раскладке, к заказу 2,16 м²; пом. 4; л. 54–57
Сухие смеси и гидроизоляция											
6	Клей плиточный цементный класса C2 TE S1 (ГОСТ Р 56387-2018)	Ceresit CM 17 или аналог			кг	535,99	10	мешок 25 кг	24 меш.	25	слой 5 мм, 1,50 кг/м² на 1 мм; л. 54
7	Затирка цементная класса CG2WA, цвет — по колерной карте	Mapei Ultracolor Plus 132 или аналог			кг	5,44	10	упак. 2 кг	3 упак.	2	расход (a+b)/ab × шов × t × 1,6 кг/м²; л. 54
8	Гидроизоляция обмазочная полимерная, 2 слоя, лента в углах, манжеты на выводах	по выбору подрядчика			м²	30,02	10	ведро по ТУ	по ТУ		пом. 7, 9; расход кг/м² — по ТУ; л. 54
9	Лента демпферная по периметру пола из плитки	по выбору подрядчика			м	25,44	10	рулон	28,00 м		л. 54
10	Смесь цементно-песчаная для стяжки М200 (50 мм, 33 мм)	по выбору подрядчика			м³	6,19	5	мешок по ТУ	по ТУ		S 128,30 м² × толщина; армирование и маяки — по ТУ; л. 58
11	Смесь штукатурная гипсовая для машинного и ручного нанесения по маякам, слой до 10 мм	по выбору подрядчика			м²	287,56	10	мешок по ТУ	по ТУ		пом. 1, 2, 3, 4, 5, 6, 7, 8, 9; расход кг/м² на 1 мм слоя — по ТУ смеси, толщина — по замеру кривизны стен; л. 15, 59, 60
Короба из ГКЛВ											
12	Лист ГКЛВ 12,5 мм, 2500 × 1200 мм, обшивка коробов в 2 слоя	по выбору подрядчика			м²	8,50	10	лист 3,00 м²	4,00 лист		инсталляция пом. 7: 2,78 м²; инсталляция пом. 9: 1,47 м²; площадь × 2 слоя; короб К1 над полом — в спецификации ВК; л. 36, 54–57
13	Профиль стальной оцинкованный 27 × 28 мм: каркас коробов (стойки и направляющие)	по выбору подрядчика			м	18,20	10	хлыст 3 м	7 шт		стойки через 400 мм по свободному периметру + направляющие по полу и потолку; крепёж, лента, шпаклёвка швов — по узлу короба; л. 36, 54–57
Слаботочные сети											
14	Кабель домофона — тип по системе поставщика	по выбору подрядчика			м	5,70		бухта по ТУ	6,00 м		по лучам от ЩС**, 1 точ., запас 10 % уже в длине; 3 точ. — предложение листа слаботочки (знак «*» на плане); л. 33
15	Кабель коаксиальный RG-6 (75 Ом) к розеткам ТВ	по выбору подрядчика			м	57,00		бухта по ТУ	57,00 м		по лучам от ЩС**, 3 точ., запас 10 % уже в длине; 3 точ. — предложение листа слаботочки (знак «*» на плане); л. 33
16	Кабель U/UTP кат. 6 (LAN, Wi-Fi и камеры по PoE)	по выбору подрядчика			м	110,60		бухта по ТУ	111,00 м		по лучам от ЩС**, 7 точ., запас 10 % уже в длине; 3 точ. — предложение листа слаботочки (знак «*» на плане); л. 33
17	Гофротруба Ø20 для слаботочных линий, отдельно от силовых	по выбору подрядчика			м	156,00		бухта по ТУ	156,00 м		по длине лучей без участков в канале плинтуса (≈ 90 %); л. 33
18	Розетка компьютерная RJ45, кат. 6, с рамкой и подрозетником	по выбору подрядчика			шт	5		шт	5 шт		LAN2–LAN5, LAN6**; серия механизмов — как у розеток и выключателей; л. 28, 29, 33

Допущения и предложения на листе

Основа листа: размеры сняты с растрового плана заказчика с частичными размерами: рисунок не в масштабе, помещения выровнены по подписанным размерам мебели и проходов; контрольный обмер не выполнен (К-1); высота потолка 2700 мм принята: на плане заказчика её нет (К-2); толщины стен 300 / 120 мм приняты по плану заказчика, не замерены (К-1); разрешённая мощность 15 кВт принята по типовым ТУ для квартиры, ТУ заказчиком не переданы (К-4); подрайон климата не задан — принят не северный (жилые от 2,5 м) (К-6). Знак «**» — предложение проектировщика, заказчиком не утверждено (согласовать с заказчиком): LAN6 — стол К62 стоит посреди помещения — питание из лючка в полу под столом: трасса в конструкции пола (толщина стяжки — по обмеру) — согласовать с заказчиком; ЩС — щит слаботочный: место и состав; плинтус пом. 1–5, 8, фартук пом. 4 — артикул изделия не выбран: позиция описана характеристиками («аналог по характеристикам»), артикул выбирается при закупке; пол пом. 7, 9 — пирог пола: стяжка 33 мм и обмазочная гидроизоляция добавлены разработчиком проекта; артикул изделия не выбран: позиция описана характеристиками («аналог по характеристикам»), артикул выбирается при закупке. См. лист открытых вопросов (лист 6, записи К-1, К-2, К-4, К-6).

Изм.	Кол.уч	Лист	№ док.	Подп.	Дата
Разраб.		Кырлан А.С.			04.11.26
Пров.					
ГИП					
Н. контр.					
Утв.					

ГД-2026-008-АИ

Квартира с кабинетом

Общая площадь 127,29* м² · * размеры со скана, не замерены (реестр — л. 6–8, К-1)

Стадия	Лист	Листов
РП	128	131

Дизайн-проект интерьера

Спецификация материалов

М б/м

Кырлан Александр Сергеевич

Спецификация материалов (окончание)

Отделочные материалы: чистое количество, запас, упаковка, к заказу · ГОСТ 21.110-2013

Спецификация материалов (ГОСТ 21.110-2013, форма 1) (продолжение)

Поз.	Наименование и техническая характеристика	Тип, марка, артикул	Код продукции	Поставщик	Ед. изм.	Количество				Масса ед., кг	Примечание
						чистое	запас, %	упаковка	к заказу		
19	Розетка телевизионная (коаксиальная) с рамкой и подрозетником	по выбору подрядчика			шт	3		шт	3 шт		ТВ1, ТВ2, ТВ4; серия механизмов — как у розеток и выключателей; л. 28, 29, 33
20	Трубка или монитор домофона (поставка домофонной организации)	по выбору подрядчика			шт	1		шт	1 шт		ДФ1; серия механизмов — как у розеток и выключателей; л. 28, 29, 33
21	Щит слаботочный ЩС**: корпус, DIN-рейка, розетки 220 В	по выбору подрядчика			шт	1		шт	1 шт		ЩС**; серия механизмов — как у розеток и выключателей; л. 28, 29, 33
22	Патч-панель, портов не менее 7	по выбору подрядчика			шт	1		шт	1 шт		серия механизмов — как у розеток и выключателей; л. 28, 29, 33
Лакокрасочные материалы											
23	Краска интерьерная акриловая, матовая, класс истирания 1	Farrow & Ball Modern Emulsion No. 34 «Calke Green — традиционный шалфей»			л	8,14	10	банка 2,5 л	4 банк		33,93 м² × 2 сл. × 0,12 л/м²; пом. 1, 3, 4, 6; л. 59, 60
24	Краска интерьерная акриловая, матовая, класс истирания 1	Farrow & Ball Modern Emulsion No. 15 «Bone мягкий каменно-серый с зеленцой»			л	43,15	10	банка 2,5 л	19 банк		179,79 м² × 2 сл. × 0,12 л/м²; пом. 1, 3, 4, 5, 6, 8; л. 59, 60
25	Краска интерьерная акриловая, глубокоматовая, класс истирания 2	Tikkurila Anti-Reflex 2 V503 «Winter»			л	27,45	10	банка 2,7 л	12 банк		114,36 м² × 2 сл. × 0,12 л/м²; пом. 1 (пот.), 2 (пот.), 3 (пот.), 4 (пот.), 5 (пот.), 6 (пот.), 8 (пот.); л. 59, 60
26	Краска интерьерная акриловая, матовая, класс истирания 1	Tikkurila Harmony V503 «Winter»			л	5,51	10	банка 2,7 л	3 банк		22,94 м² × 2 сл. × 0,12 л/м²; пом. 2; л. 59, 60
27	Краска интерьерная акриловая, матовая, класс истирания 1	Tikkurila Luja 7 V503 «Winter»			л	3,10	10	банка 2,7 л	2 банк		12,93 м² × 2 сл. × 0,12 л/м²; пом. 7 (пот.), 9 (пот.); л. 59, 60
28	Шпаклёвка финишная полимерная под окраску (стены и потолки, Q3)	по выбору подрядчика			м²	363,95	10	ведро по ТУ	по ТУ		расход кг/м² на слой — по ТУ; л. 59, 60
29	Грунтовка акриловая глубокого проникновения, 2 слоя	по выбору подрядчика			м²	414,85	10	канистра по ТУ	по ТУ		расход л/м² — по ТУ; л. 59, 60
Погонажные изделия и потолки											
30	Плинтус напольный МДФ под покраску, h=80 мм, крепление к стене	аналог: плинтус МДФ под покраску 80×16			м.п.	85,38	10	хлыст 2,4 м	40 шт		пом. 1, 2, 3, 4, 5, 8; длина хлыста — по артикулу; л. 59, 60
31	Плинтус напольный МДФ под покраску, h=69 мм, крепление к стене	SX165			м.п.	11,96	10	хлыст 2,4 м	6 шт		пом. 6; длина хлыста — по артикулу; л. 59, 60
32	Потолок подвесной ГКЛ/ГКЛВ по каркасу Knauf П113: листы, профили, подвесы, лента, шпаклёвка швов	Knauf П113			м²	122,18		комплект	по л. потолков		площадь — по ведомости потолков; число листов, профилей и подвесов — по шагам каркаса на листе потолков; л. 48–53

Примечания

1. Чистое количество — из ведомости объёмов работ и раскладки плитки; запас — отдельной графой (доска — по ведомости отделки, плитка, краска и плинтус — 10 %); «к заказу» — с запасом и кратно упаковке.
2. Плитка — штуками по раскладке, запас на каждую поверхность. Калибр (рабочий размер) и тон — одной партией на помещение, калибр указать при заказе и сверить с раскладкой до укладки.
3. Краска — 0,12 л/м² на слой (середина вилки 0,10–0,15 л/м²) по фактической площади окраски из ведомости отделки; колеровка одной партией.
4. «По ТУ» — расход задаёт производитель выбранного продукта; количество к заказу — после выбора марки.
5. Поз. 3, 5, 30 заданы характеристиками («аналог:»): марку, артикул и поставщика согласовать с заказчиком до закупки, без артикула не заказывать.
6. Штукатурная смесь — на ту же площадь, что строка ВОР «Штукатурка стен» (287,56 м²): площадь одна, расход смеси задаёт производитель.
7. Коробы инсталляции и стояков: ГКЛВ в 2 слоя и профиль 27 × 28 мм считаются по свободным граням коробов (источник — раскладка плиточника и шахты в данных); короб К1 над полом — в спецификации ВК.
8. Потолки ГКЛ: в этой спецификации — площадь системы П113; число листов, профилей и подвесов — по шагам каркаса на листе потолков (подвесы через 1000, несущие через 500, основные через 1200 мм), схема каркаса не выпущена. Сантехника, светильники и мебель — по своим спецификациям.

Допущения и предложения на листе

Основа листа: размеры сняты с растрового плана заказчика с частичными размерами: рисунок не в масштабе, помещения выровнены по подписанным размерам мебели и проходов; контрольный обмер не выполнен (К-1); высота потолка 2700 мм принята: на плане заказчика её нет (К-2); толщины стен 300 / 120 мм приняты по плану заказчика, не замерены (К-1); разрешённая мощность 15 кВт принята по типовым ТУ для квартиры, ТУ заказчиком не переданы (К-4); подрайон климата не задан — принят не северный (жилые от 2,5 м) (К-6). Знак «**» — предложение проектировщика, заказчиком не утверждено (согласовать с заказчиком): ЩС — щит слаботочный: место и состав; плинтус пом. 1–5, 8, фартук пом. 4 — артикул изделия не выбран: позиция описана характеристиками («аналог по характеристикам»), артикул выбирается при закупке; пол пом. 7, 9 — пирог пола: стяжка 33 мм и обмазочная гидроизоляция добавлены разработчиком проекта; артикул изделия не выбран: позиция описана характеристиками («аналог по характеристикам»), артикул выбирается при закупке.

См. лист открытых вопросов (лист 6, записи К-1, К-2, К-4, К-6).

Изм.	Кол.уч	Лист	№ док.	Подп.	Дата
Разраб.		Кырлан А.С.			04.11.26
Пров.					
ГИП					
Н. контр.					
Утв.					

ГД-2026-008-АИ

Квартира с кабинетом

Общая площадь 127,29* м² · * размеры со скана, не замерены (реестр — л. 6–8, К-1)

Дизайн-проект интерьера	Стадия	Лист	Листов
	РП	129	131

Спецификация материалов (окончание)

М б/м

Кырлан Александр Сергеевич

Смета ориентировочная

ПРЕДВАРИТЕЛЬНО · не для производства работ · открыто пунктов: 13 (реестр — л. 6–8)

Работы, материалы, оборудование, услуги и резерв · цены — ориентир по открытым прайсам, не коммерческое предложение

Сводная смета (цены на 21.09.2026, Москва)

№	Наименование работ, материалов, услуг	Ед. изм.	Кол-во	Цена за ед., ₽	Стоимость, ₽			Чей подряд	Срок поставки, дн.	Основание	Источник цены
					план	факт	разница				
Работы — по ведомости объёмов работ											
1	Демонтаж и черновые работы (без 5 поз. по КП)	раздел	1		422 185			бригада		ВОР, поз. 1–10; л. 125–127	по ВОР
2	Инженерные системы (без 13 поз. по КП)	раздел	1		211 373			бригада		ВОР, поз. 11–34; л. 125–127	по ВОР
3	Чистовые работы (без 1 поз. по КП)	раздел	1		900 115			бригада, поставщик		ВОР, поз. 35–52; л. 125–127	по ВОР
Материалы — по спецификации материалов											
4	Инженерная доска	м²	114,60	4 513	517 190			поставщик		спецификация, поз. 1	Ц7
5	Керамогранит 600×600 мм	м²	18,36	1 800	33 048			поставщик		спецификация, поз. 3	Ц6
6	Керамогранит 600×1200, 1200×600 мм	м²	113,76	3 500	398 160			поставщик		спецификация, поз. 4, 5	Ц6
7	Клей плиточный цементный класса C2 TE S1	меш.	24	1 800	43 200			поставщик		спецификация, поз. 6	Ц7
8	Затирка цементная класса CG2WA	упак.	3	1 000	3 000			поставщик		спецификация, поз. 7	Ц7
9	Краска Farrow & Ball Modern Emulsion, банка 2,5 л	банк	23	5 800	133 400			поставщик		спецификация, поз. 23, 24	Ц7
10	Краска Tikkurila (Anti-Reflex 2, Harmony, Luja 7), банка 2,7 л	банк	17	3 510	59 670			поставщик		спецификация, поз. 25, 26, 27	Ц6
11	Плинтус напольный МДФ под покраску	шт	46	368	16 928			поставщик		спецификация, поз. 30, 31	Ц7
12	Прочие материалы с расходом по ТУ (клей для доски, гидроизоляция, демпферная лента, смесь для стяжки, смесь штукатурная гипсовая для машинного и ручного нанесения по маякам, лист гклв 12, профиль стальной оцинкованный 27 × 28 мм: каркас коробов (стойки и направляющие), кабель слаботочки, гофра слаботочки, изделия слаботочки, шпаклёвка, грунтовка, каркас и ГКЛ потолков)	компл	1	по КП				поставщик		спецификация, поз. 2, 8, 9, 10, 11, 12, 13, 14, 15, 16, 17, 18, 19, 20, 21, 22, 28, 29, 32	
Оборудование и мебель — поставка по спецификациям											
13	Кухонный гарнитур по проекту кухни, изготовление и монтаж (4–8 нед.)	компл	1	по КП				поставщик	не задан; ориентир 4–8 нед. от замера	л. 78, 79	

Допущения и предложения на листе

Основа листа: размеры сняты с растрового плана заказчика с частичными размерами: рисунок не в масштабе, помещения выровнены по подписанным размерам мебели и проходов; контрольный обмер не выполнен (К-1); высота потолка 2700 мм принята: на плане заказчика её нет (К-2); толщины стен 300 / 120 мм приняты по плану заказчика, не замерены (К-1); разрешённая мощность 15 кВт принята по типовым ТУ для квартиры, ТУ заказчиком не переданы (К-4); подрайон климата не задан — принят не северный (жилые от 2,5 м) (К-6).
См. лист открытых вопросов (лист 6, записи К-1, К-2, К-4, К-6).

Изм.	Кол.уч	Лист	№ док.	Подп.	Дата
Разраб.		Кырлан А.С.			04.11.26
Пров.					
ГИП					
Н. контр.					
Утв.					

ГД-2026-008-АИ

Квартира с кабинетом

Общая площадь 127,29* м² · * размеры со скана, не замерены (реестр — л. 6–8, К-1)

Дизайн-проект интерьера

Стадия	Лист	Листов
РП	130	131

Смета ориентировочная

М б/м

Кырлан Александр Сергеевич

Смета ориентировочная (окончание)

ПРЕДВАРИТЕЛЬНО · не для производства работ · открыто пунктов: 13 (реестр — л. 6–8)

Работы, материалы, оборудование, услуги и резерв · цены — ориентир по открытым прайсам, не коммерческое предложение

Сводная смета (цены на 21.09.2026, Москва) (продолжение)

№	Наименование работ, материалов, услуг	Ед. изм.	Кол-во	Цена за ед., ₽	Стоимость, ₽			Чей подряд	Срок поставки, дн.	Основание	Источник цены
					план	факт	разница				
14	Двери скрытого монтажа с коробом под покраску, поставка	шт	6	по КП				поставщик	не задан; ориентир ≈ 30 дн.	л. 17, 18	
15	Оборудование заказчика слаботочных сетей: точка доступа wi-fi — 2 шт; коммутатор — 1 шт	компл	1	по КП				заказчик		л. 28, 29	
16	Сантехника, светильники, мебель и предметы интерьера	компл	1	по КП				поставщик		л. 46; л. 47; л. 83; л. 21–24	
Прочие работы и услуги											
17	Вынос и вывоз строительного мусора	м³		по факту				бригада		после демонтажа	
18	Подъём материалов на этаж (лифтом или вручную — по договору)	т		по факту				бригада		по массе поставки	
19	Доставка чистовых материалов, 10 % от поставки			10 %	120 460			поставщик		от суммы материалов	
20	Уборка после ремонта	м²	127,29	по факту				бригада		S квартиры	
	Итого работы				**1 533 673**						
	Итого материалы				**1 204 596**						
	Итого прочие услуги				**120 460**						
	Резерв на непредвиденные работы и материалы, 15 %				**428 809**						
	ВСЕГО ориентировочно (без оборудования и позиций по КП)				**3 287 538**						

Примечания

1. Смета ориентировочная, не коммерческое предложение: объёмы — из ведомости объёмов работ и спецификации материалов, цены — нижняя граница открытых прайсов Москвы (цены на 21.09.2026); перед договором цены подтвердить у подрядчика и поставщиков.
2. Источники цен: Ц1 — Домашний мастерок: прайс на отделочные работы, 2026; Ц2 — Домашний мастерок: прайс на плиточные работы, 2026; Ц3 Домашний мастерок: прайс на электромонтажные работы, 2026; Ц4 — Профи ремонтник: штукатурно-малярные работы; Ц5 — Profi.ru: укладка керамогранита на стены, Москва 2026; Ц6 — knowledge/spec-materials.md, разд. 1 и 3: ориентир по сегментам; Ц7 — Розница Москвы, 09.2026: Лемана ПРО, KGSnab, официальный дилер Farrow & Ball.
3. В итог не вошли позиции «по КП» и «по факту»: оборудование и мебель, двери, материалы с расходом по ТУ, вывоз мусора, подъём и уборка.
4. Доставка — 10 % от материалов, резерв — 15 % (частный ремонт 10–20 %) отдельными строками, в количествах не спрятаны. Графы «факт» и «разница» заполняются по актам.

Допущения и предложения на листе

Основа листа: размеры сняты с растрового плана заказчика с частичными размерами: рисунок не в масштабе, помещения выровнены по подписанным размерам мебели и проходов; контрольный обмер не выполнен (К-1); высота потолка 2700 мм принята: на плане заказчика её нет (К-2); толщины стен 300 / 120 мм приняты по плану заказчика, не замерены (К-1); разрешённая мощность 15 кВт принята по типовым ТУ для квартиры, ТУ заказчиком не переданы (К-4); подрайон климата не задан — принят не северный (жилые от 2,5 м) (К-6).
См. лист открытых вопросов (лист 6, записи К-1, К-2, К-4, К-6).

Изм.	Кол.уч	Лист	№ док.	Подп.	Дата
Разраб.		Кырлан А.С.			04.11.26
Пров.					
ГИП					
Н. контр.					
Утв.					

ГД-2026-008-АИ

Квартира с кабинетом

Общая площадь 127,29* м² · * размеры со скана, не замерены (реестр — л. 6–8, К-1)


Дизайн-проект интерьера	Стадия	Лист	Листов
	РП	131	131
Смета ориентировочная (окончание) М б/м	**Кырлан Александр Сергеевич**		

11

Визуализации

Кырлан Александр Сергеевич

выпуск 04.11.2026 № 4177cbe7a3 · стр. 142 из 166

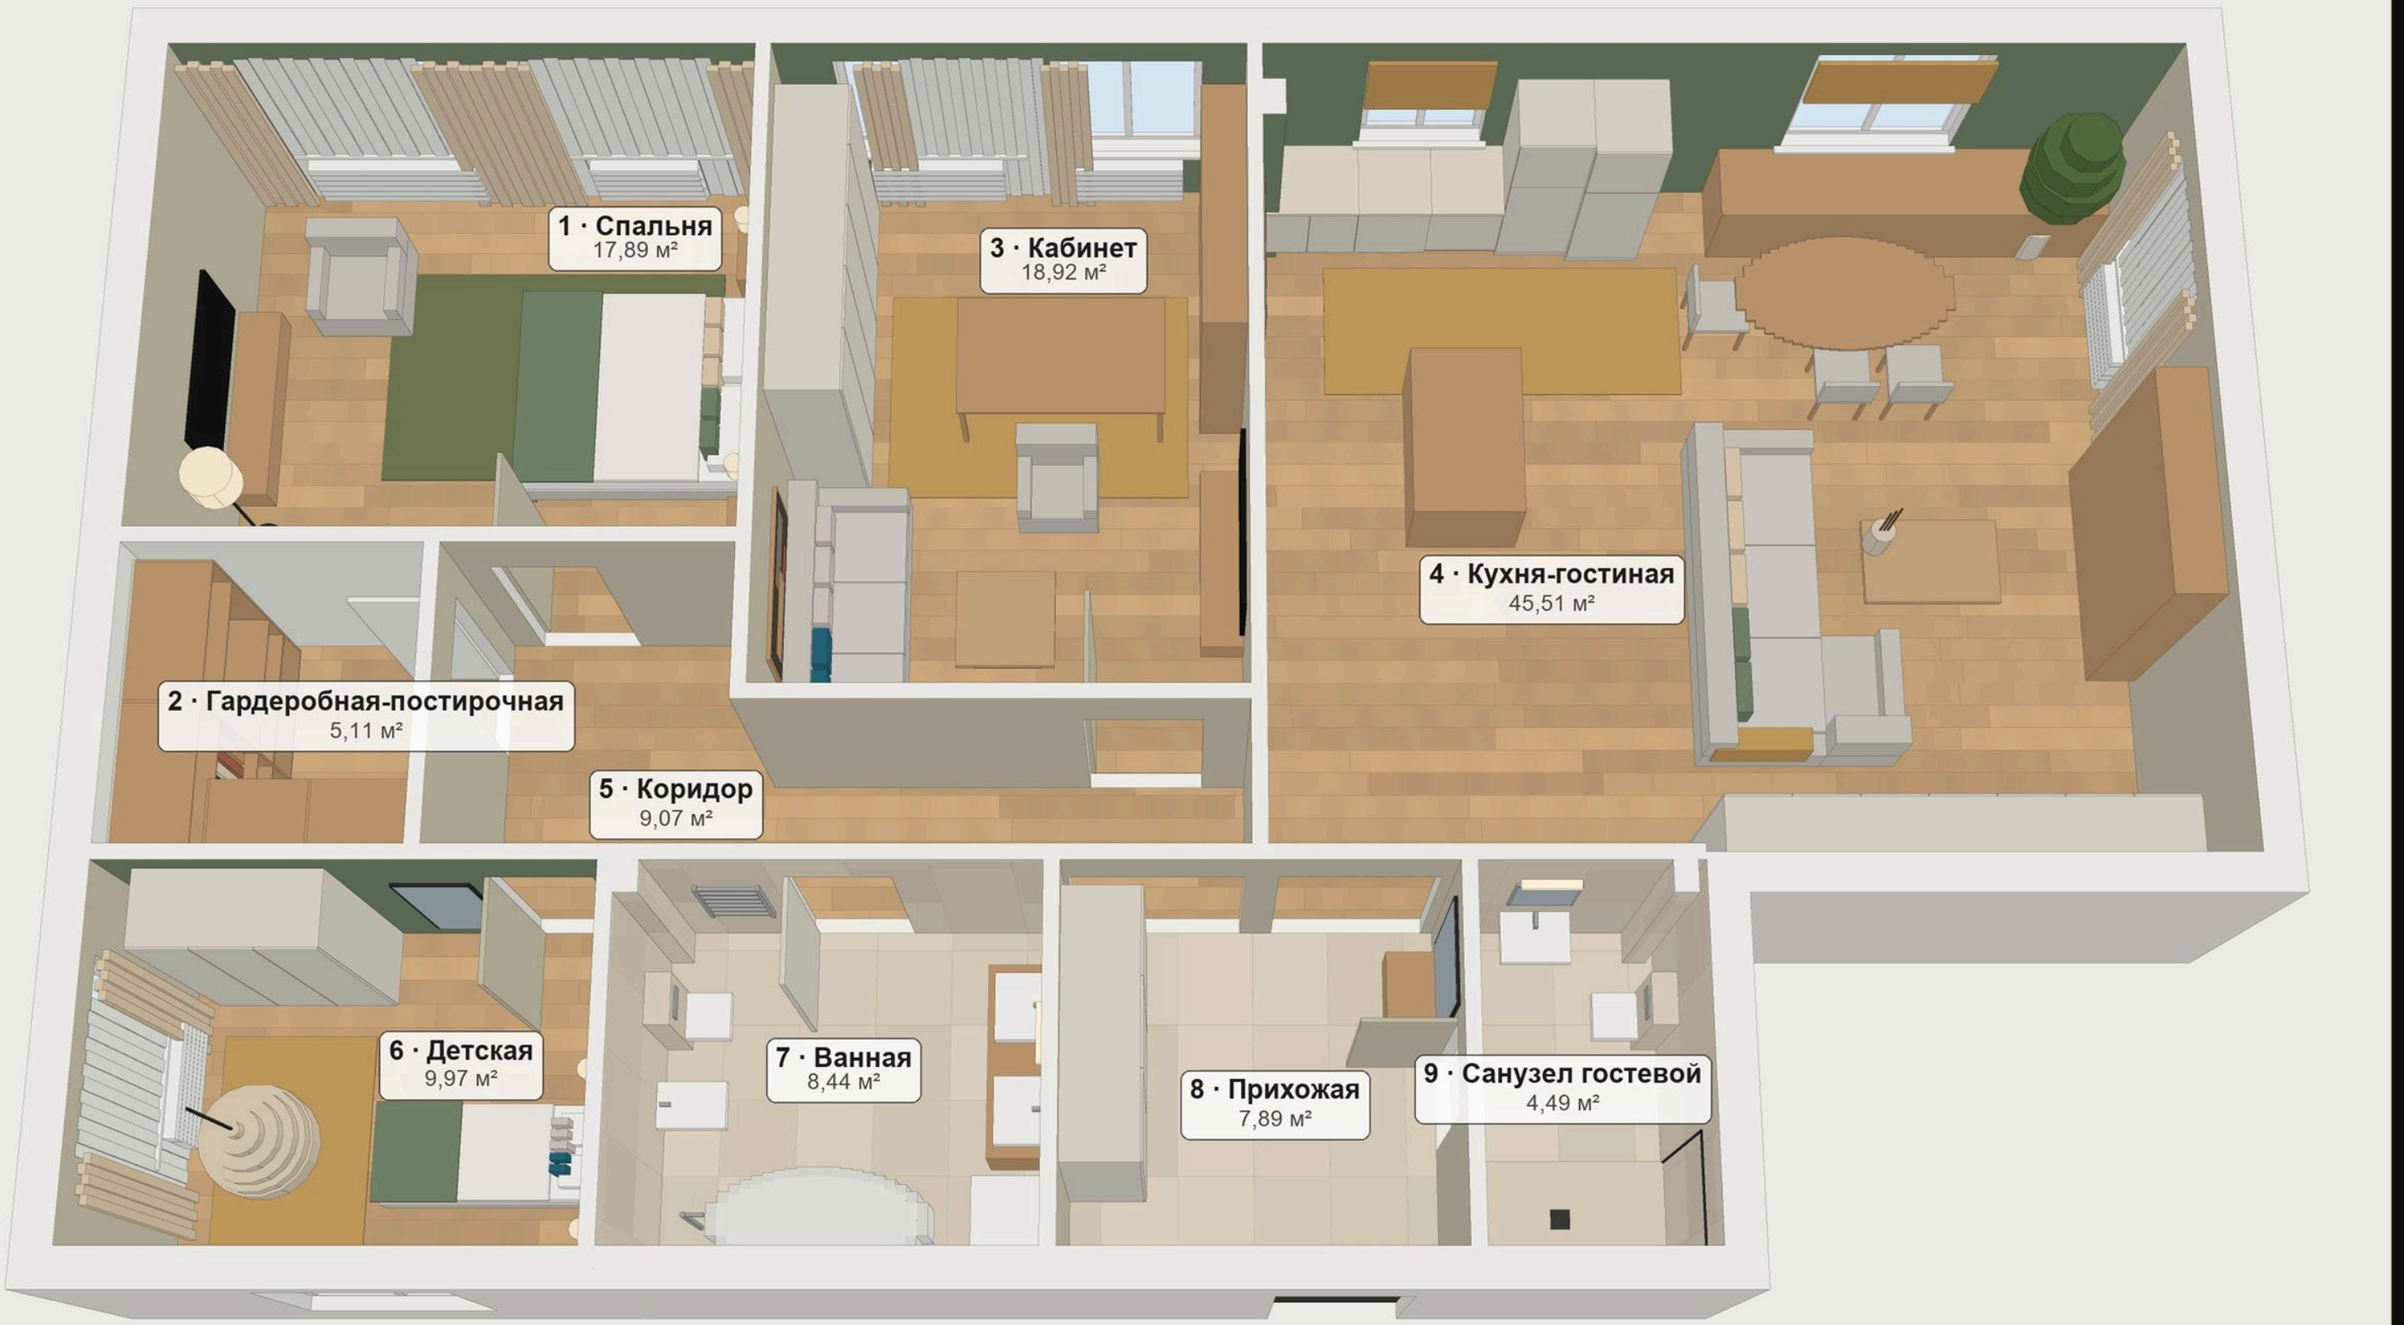

Планировочное решение · вид сверху

выпуск 04.11.2026 № 4177cbe7a3 · стр. 143 из 166

выпуск 04.11.2026 № 4177cbe7a3 · стр. 144 из 166

Ванная · стена Б



Ванная · стена B

выпуск 04.11.2026 № 4177cbe7a3 · стр. 145 из 166



Ванная · стена Г

выпуск 04.11.2026 № 4177cbe7a3 · стр. 146 из 166



Санузел гостевой · стена B

Квартира с кабинетом · визуализация 5 из 24

выпуск 04.11.2026 № 4177cbe7a3 · стр. 147 из 166

выпуск 04.11.2026 № 4177cbe7a3 · стр. 148 из 166



Санузел гостевой · общий вид

выпуск 04.11.2026 № 4177cbe7a3 · стр. 149 из 166

Спальня · стена А

выпуск 04.11.2026 № 4177cbe7a3 · стр. 150 из 166



Спальня · стена Б



Спальня · стена Г

выпуск 04.11.2026 № 4177cbe7a3 · стр. 151 из 166



Коридор · стена B

выпуск 04.11.2026 № 417/cbe7a3 · стр. 152 из 166



Прихожая · стена Б

выпуск 04.11.2026 № 4177cbe7a3 · стр. 153 из 166



Прихожая · стена B

выпуск 04.11.2026 № 4177cbe7a3 · стр. 154 из 166



Прихожая · стена Г

выпуск 04.11.2026 № 4177cbe7a3 · стр. 155 из 166



Детская · стена А

Квартира с кабинетом · визуализация 14 из 24

выпуск 04.11.2026 № 4177cbe7a3 · стр. 156 из 166



Детская · стена Б

Квартира с кабинетом · визуализация 15 из 24

выпуск 04.11.2026 № 4177cbe7a3 · стр. 157 из 166

выпуск 04.11.2026 № 4177cbe7a3 · стр. 158 из 166

Детская · стена Г

выпуск 04.11.2026 № 4177cbe7a3 · стр. 159 из 166



Кухня-гостиная · стена А



Кухня-гостиная · стена Б

выпуск 04.11.2026 № 417cbe7a3 · стр. 160 из 166



Кухня-гостиная · стена B

Квартира с кабинетом · визуализация 19 из 24

выпуск 04.11.2026 № 4177cbe7a3 · стр. 161 из 166



Кухня-гостиная · стена Г

выпуск 04.11.2026 № 417/cbe7a3 · стр. 162 из 166

выпуск 04.11.2026 № 4177cbe7a3 · стр. 163 из 166




Кабинет · стена А



Кабинет · стена Б

выпуск 04.11.2026 № 4177cbe7a3 · стр. 164 из 166

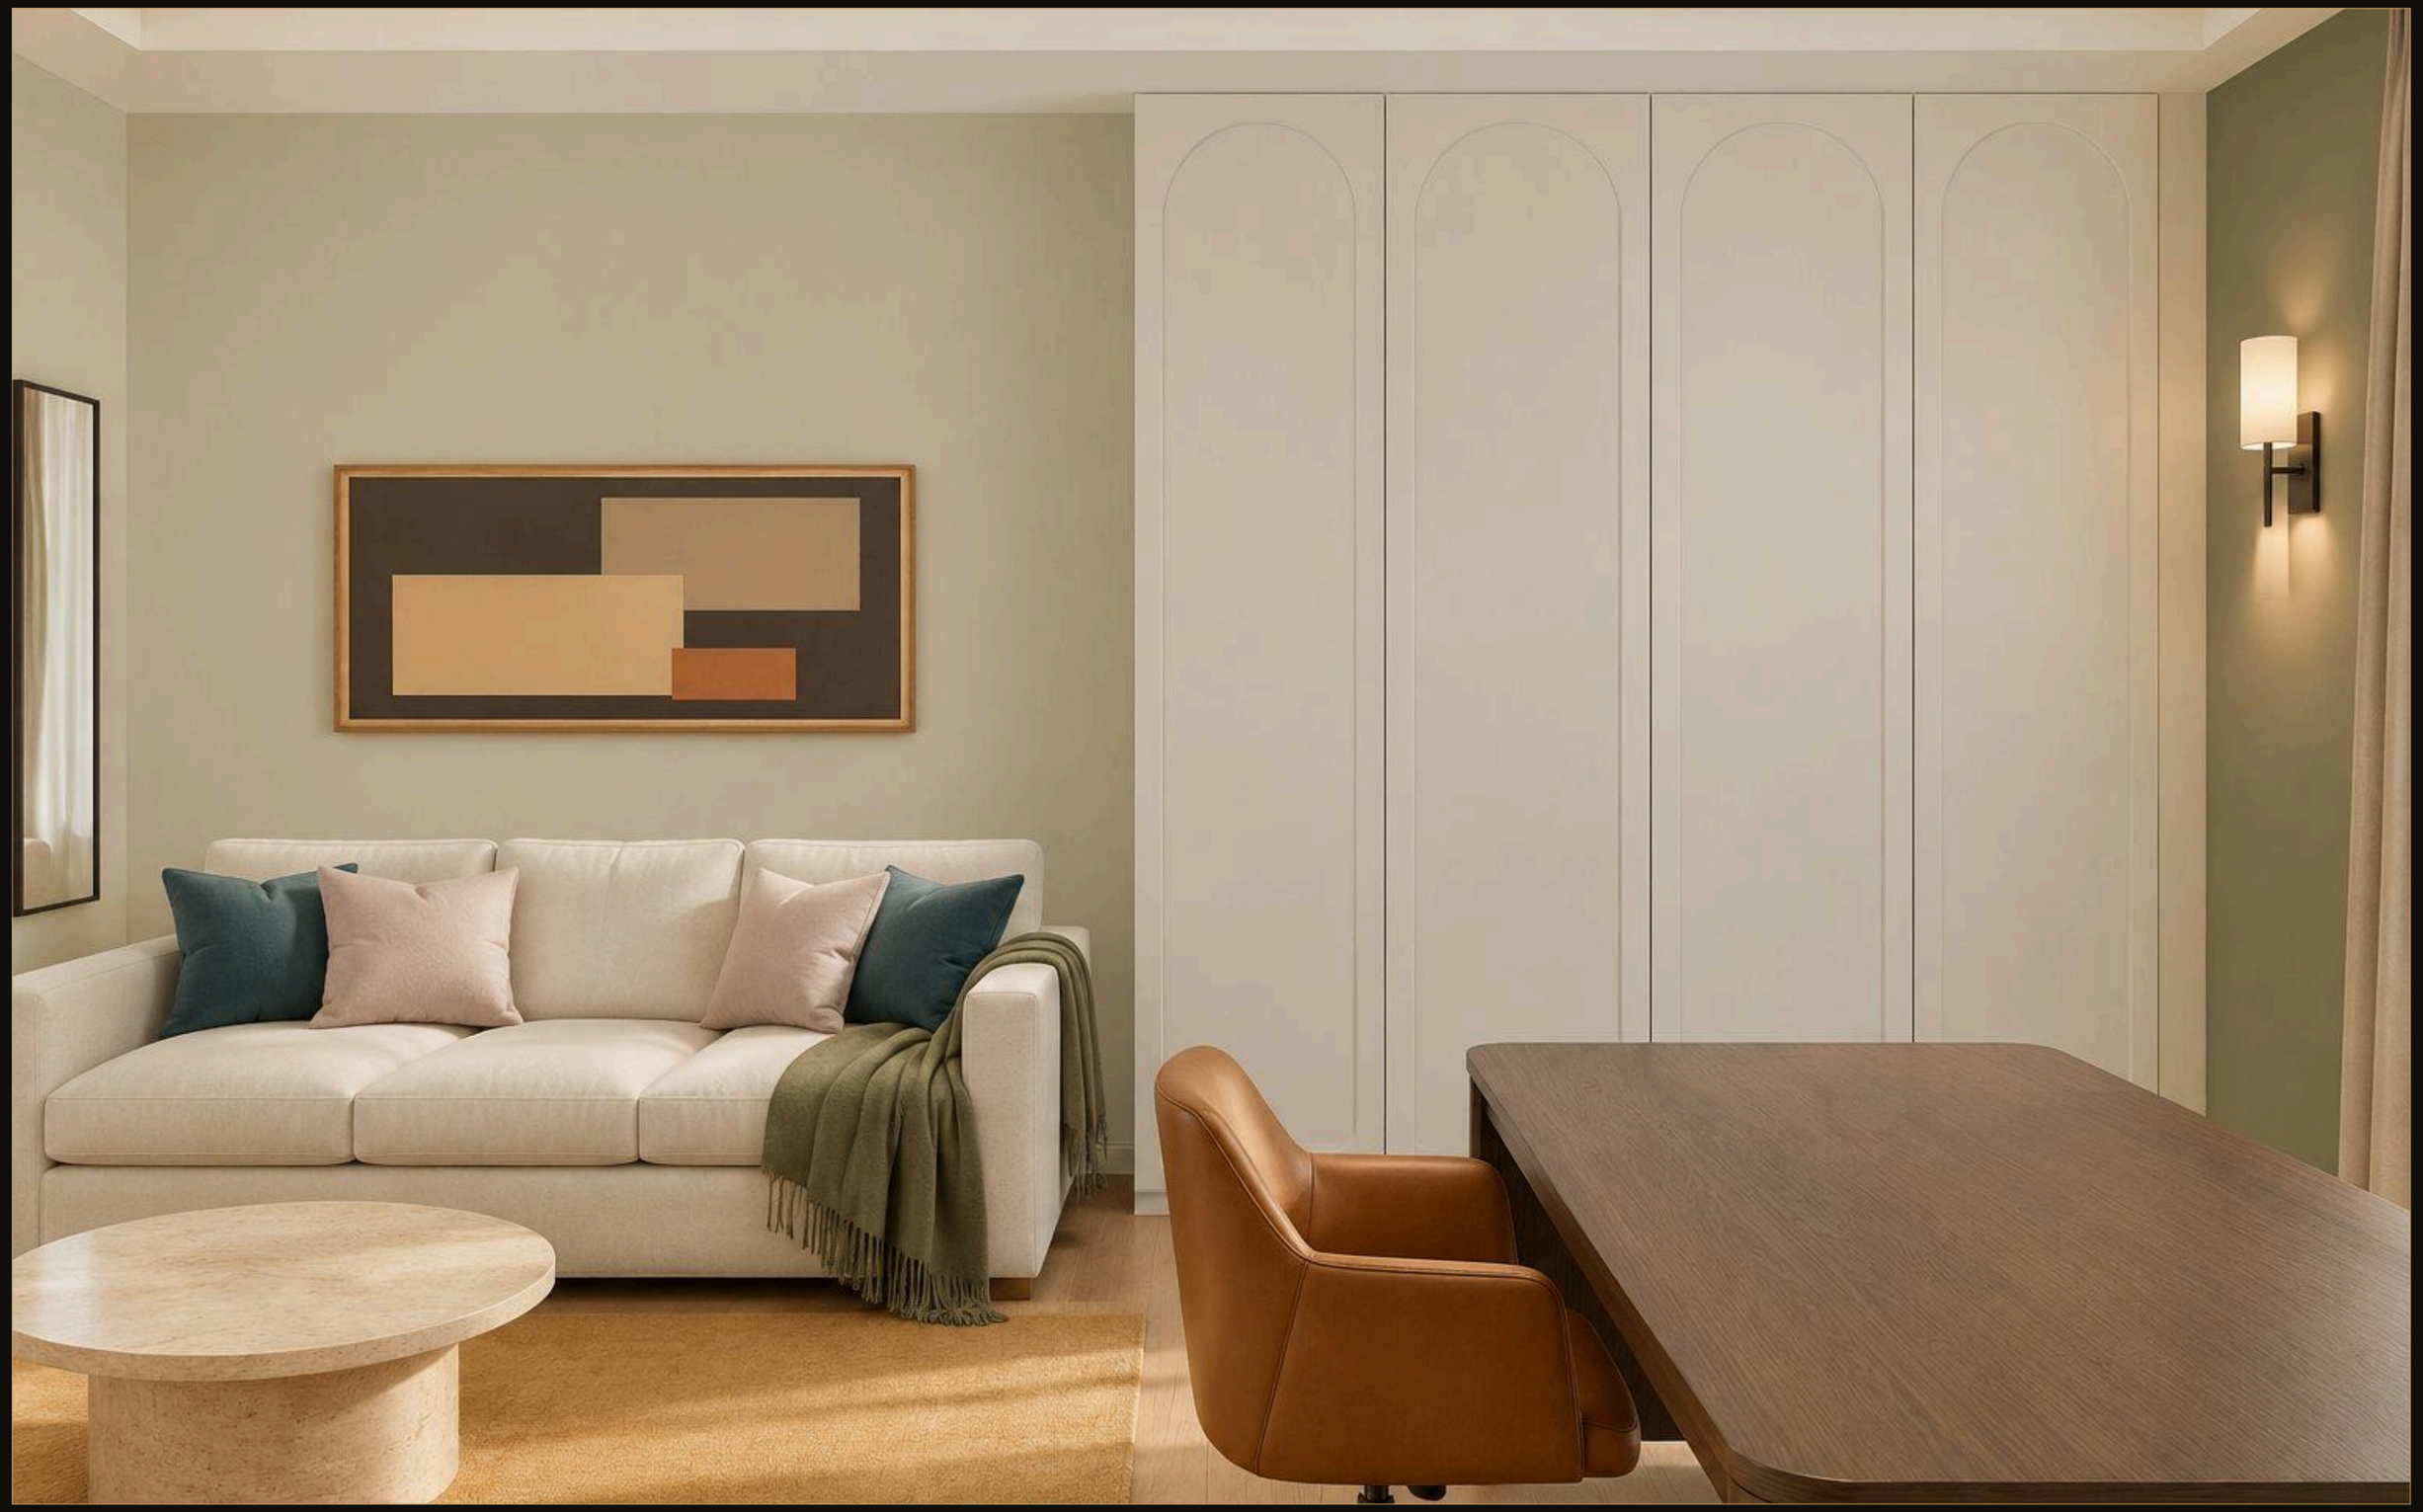

Кабинет · стена Г

выпуск 04.11.2026 № 4177cbe7a3 · стр. 165 из 166



Гардеробная-постирочная · общий вид

выпуск 04.11.2026 № 4177cbe7a3 · стр. 166 из 166