
Замерный лист · квартира

LINEA · все размеры в мм · стены A верх / B право / C низ / D лево — одной ориентацией на всю квартиру

Адрес	
Заказ / объект	
Кто мерил (Ф. И. О.)	
Дата · начало–конец	. .20 : – :
Инструмент	
Этаж / этажей в доме	/
Площадь по документам	м²

Тип дома	☐ панель ☐ кирпич ☐ монолит ☐ блок
Серия · год	
Откуда известно	☐ проект/БТИ ☐ со слов ☐ по виду
Давление ХВС (манометр)	бар · где:
Ввод воды, счётчики	пом. № ☐ счётчики · фото №
Электрощит: где · низ	пом. № от ст. от ст. h
Вводной автомат · модули	А, хар. · мест занято ☐ УЗО на вводе
ТУ на мощность	☐ есть: кВт ☐ нет (не пишем мощность)

ЭСКИЗ КВАРТИРЫ (КЛЕТКА 5 ММ) · НОМЕРА ПОМЕЩЕНИЙ ПО ОБХОДУ ОТ ВХОДА ПО ЧАСОВОЙ СТРЕЛКЕ

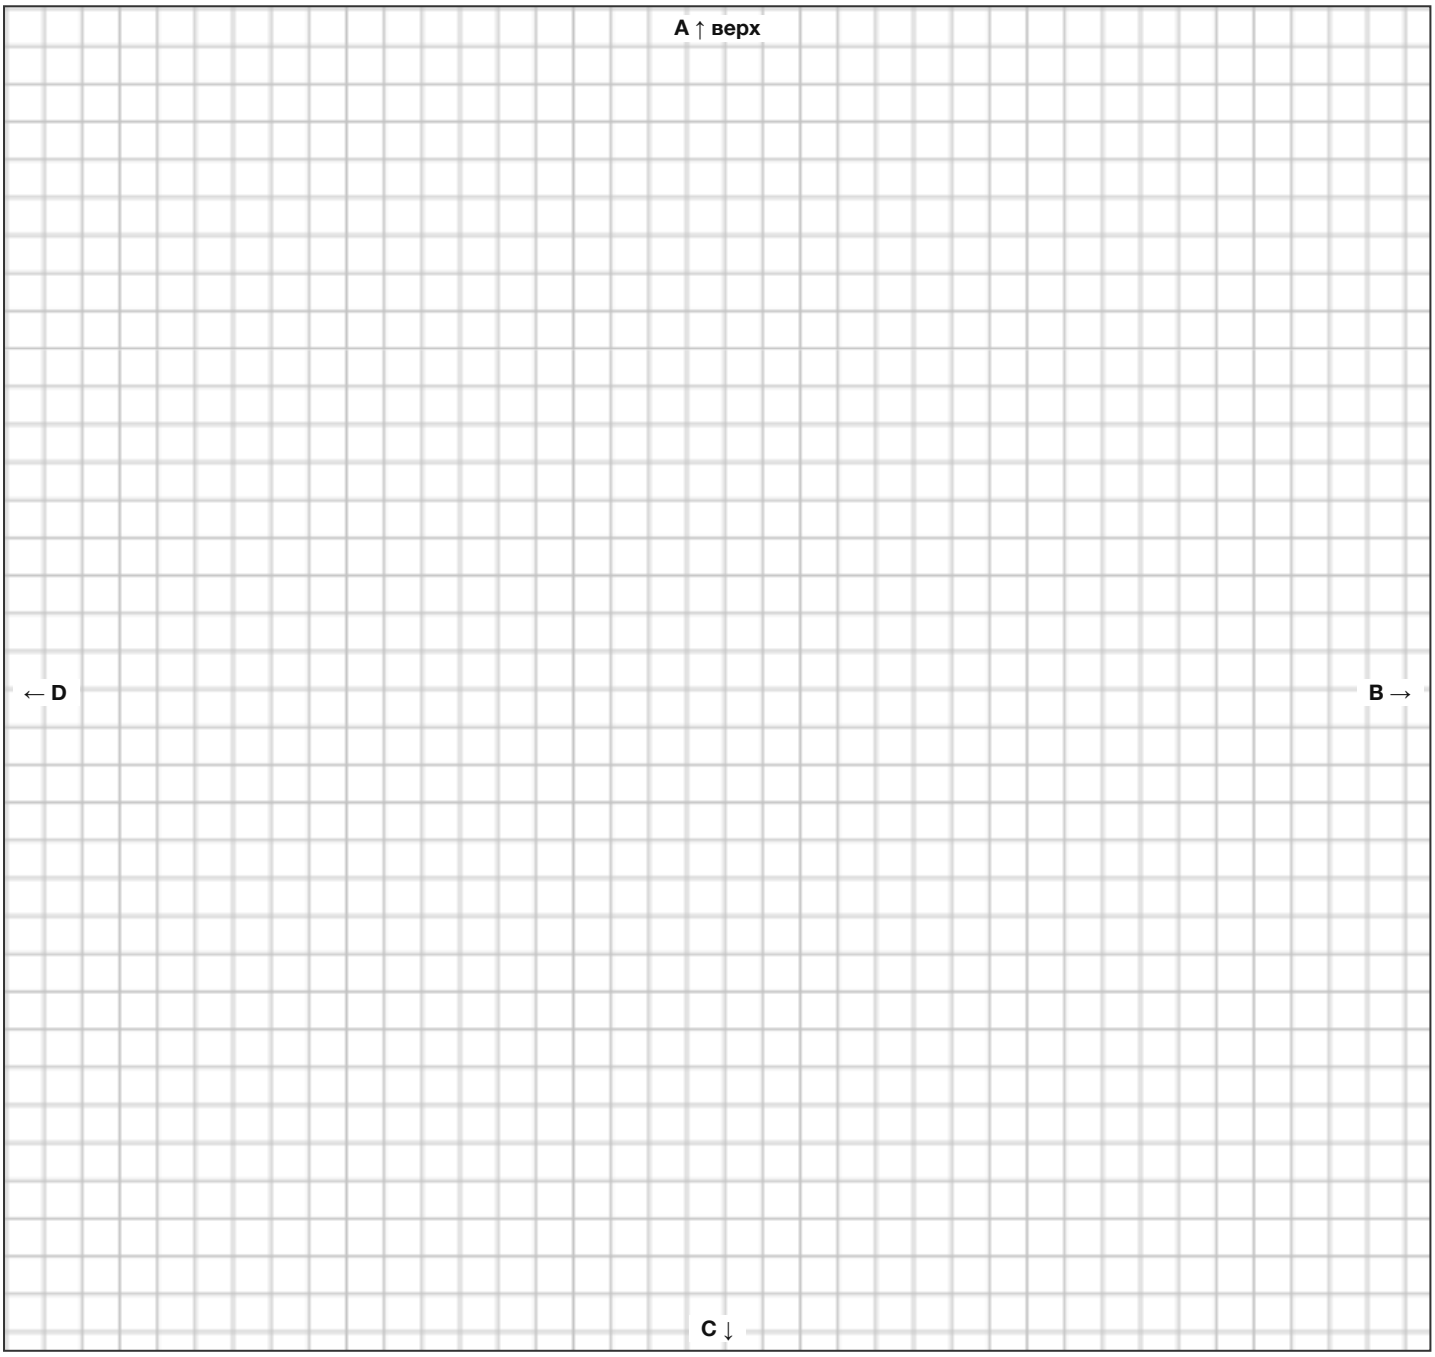

На эскизе: номер помещения, вход в квартиру, окна, стояки (К1, В1, Т3), вентканалы (ВК), щит (Щ), радиаторы (Р), балки и короба пунктиром. Помещение рядом с уже снятым: «за стеной __ помещения №__, сдвиг __ мм».

Подпись замерщика _____

Помещение № ____ · _____

тип: прихожая · коридор · комната · кухня · санузел · ванная · кладовая · балкон / лоджия

Положение на плане	за стеной **A B C D** помещения № ____, сдвиг вдоль этой стены _____ мм (от её левого / верхнего угла) · первое помещение — начало плана

СТЕНЫ (В ЧИСТОТЕ, ОТ УГЛА ДО УГЛА)

Стена	по низу	по верху	толщина	за стеной пом. / улица / соседи / МОП	материал бетон / кирпич / блок / ПГП / ГКЛ	как понял стук / проём / проект	фото №
A							
B							
C							
D							

Диагональ 1	Диагональ 2	Высота: центр	у окна	у двери	Перепад пола (ниже — «–»)

Проверка на месте: A ≈ C и B ≈ D (до 10 мм); диагонали между собой до 5 мм; √(ширина² + длина²) ≈ средней диагонали (до 1 %). Не сошлось — перемерить сейчас.

ПРОЁМЫ (ОТСТУП — ОТ ЛЕВОГО УГЛА ДЛЯ A, C И ОТ ВЕРХНЕГО ДЛЯ B, D ДО КРАЯ ПРОЁМА)

Тип окно / дверь / проём / балк.	Стена	от угла	ширина	высота	подоконник	откос	четверть	толщ. стены	петли / вход	фото №

СТОЯКИ (ДО ОСИ ОТ ДВУХ СТЕН) · ВЕНТКАНАЛЫ · РАДИАТОРЫ

Стояк К1 / В1 / Т3 / отоп. / газ	Ø	от ст. B/D	от ст. A/C	материал	кран	счётчик, h от пола	фото №

Вентканал: стена	до центра от угла	высота центра	отверстие ш × глуб.	короб?	тяга	фото №

Радиатор: стена	от угла	ширина	высота	глубина	от пола	от стены	секций, тип	подкл. бок/низ	Маевский / термоголовка	фото

ЭСКИЗ ПОМЕЩЕНИЯ

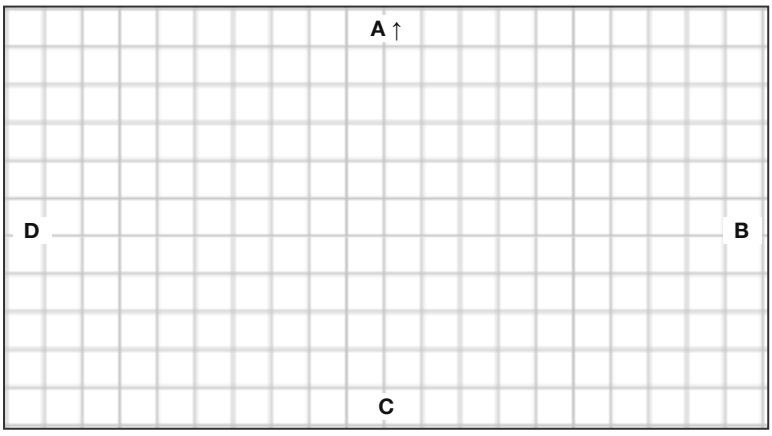


ФОТО № · ОСОБЕННОСТИ

Фото: стены
Фото: узлы
Балки, ниши, короба, трещины, сырость, плита (эл. / газ):

Помещение № ____ · _____

тип: прихожая · коридор · комната · кухня · санузел · ванная · кладовая · балкон / лоджия

Положение на плане	за стеной **A B C D** помещения № ____, сдвиг вдоль этой стены _____ мм (от её левого / верхнего угла)

СТЕНЫ (В ЧИСТОТЕ, ОТ УГЛА ДО УГЛА)

Стена	по низу	по верху	толщина	за стеной пом. / улица / соседи / МОП	материал бетон / кирпич / блок / ПГП / ГКЛ	как понял стук / проём / проект	фото №
A							
B							
C							
D							

Диагональ 1	Диагональ 2	Высота: центр	у окна	у двери	Перепад пола (ниже — «–»)

ПРОЁМЫ

Тип	Стена	от угла	ширина	высота	подоконник	откос	четверть	толщ. стены	петли / вход	фото №

СТОЯКИ · ВЕНТКАНАЛЫ · РАДИАТОРЫ

Стояк	Ø	от ст. B/D	от ст. A/C	материал	кран	счётчик, h от пола	фото №

Вентканал: стена	до центра от угла	высота центра	отверстие ш × глуб.	короб?	тяга	фото №

Радиатор: стена	от угла	ширина	высота	глубина	от пола	от стены	секций, тип	подкл. бок/низ	Маевский / термоголовка	фото

ЭСКИЗ ПОМЕЩЕНИЯ

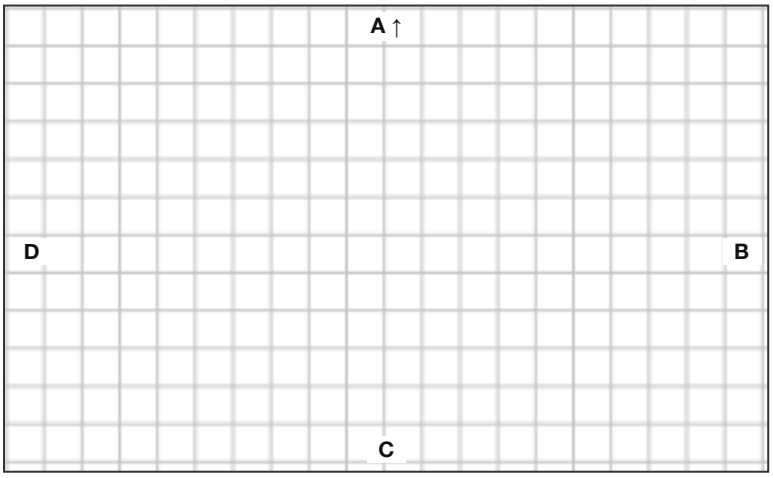


ФОТО № · ОСОБЕННОСТИ

Фото: стены
Фото: узлы
Балки, ниши, короба, трещины, сырость, плита (эл. / газ):

Перед уходом с объекта: ничего не забыл

отметить каждый пункт; «нет» — записать причину

- ☐ Каждое помещение: 4 стены по низу и по верху
- ☐ Каждое помещение: 2 диагонали, сходятся со сторонами (≤ 1 %)
- ☐ Высота потолка в 3 точках в каждом помещении
- ☐ Сумма участков стены = общей длине стены (цепочки замкнуты)
- ☐ Толщина каждой стены — в проёме или по торцу
- ☐ Каждое окно: ширина, высота, подоконник от пола, откос, четверть
- ☐ Каждая дверь: проём в чистоте ширина × высота (не полотно!), петли, порог
- ☐ Входная дверь: проём, толщина стены, сторона открывания
- ☐ Стояки: вид, Ø, ось от двух стен, материал, краны, ревизия
- ☐ Счётчики воды и краны: высота от пола, доступ
- ☐ Давление воды манометром (бар), где мерили
- ☐ Вентканалы: стена, привязка, высота, размер решётки, тяга (лист бумаги)
- ☐ Радиаторы: место, габарит, от пола и от стены, подключение, краны
- ☐ Электрощит: место, высота, вводной автомат, свободные модули; ТУ — есть / нет
- ☐ Слаботочка: ввод интернета, домофон, ТВ — где
- ☐ Газ (если есть): трубы, кран, счётчик, плита, котёл — привязки и фото
- ☐ Материал стен: простукивание, видно в проёме, по проекту — отмечено «как понял»
- ☐ Балки, колонны, ниши, короба, уступы, перепады пола — размеры и привязки
- ☐ Балкон / лоджия: размеры, высота ограждения, порог балконной двери
- ☐ Фото: каждая стена целиком + каждый узел крупно, номера вписаны
- ☐ Документы: план БТИ / проект дома / ТУ — сфотографированы или «нет»
- ☐ Эскиз: все помещения пронумерованы, привязаны «за стеной __, сдвиг __»
- ☐ Форма на телефоне: красных пунктов нет, файл скачан / отправлен
- ☐ Время окончания и подпись на листе 1

ТИПОВЫЕ ОШИБКИ (ПРОВЕРИТЬ СЕБЯ)

— Размер двери записан по полотну, а нужен проём в стене в чистоте.

— Отступ проёма от другого угла (A, C — от левого, B, D — от верхнего).

— Стены разных помещений названы по-разному: A — всегда верх общего эскиза.

— Мерили по плинтусу или мебели, а не по стене; дальномер упёрся в выступ.


— Одна диагональ «на глаз» или по сторонам — диагонали меряются прибором.

— Номинал вводного автомата записан как разрешённая мощность.

— Материал «бетон» записан без простукивания и без документа.

— Высота меряется до натяжного / подвесного потолка без отметки, что это не плита.

ЗАМЕЧАНИЯ ПО ОБЪЕКТУ

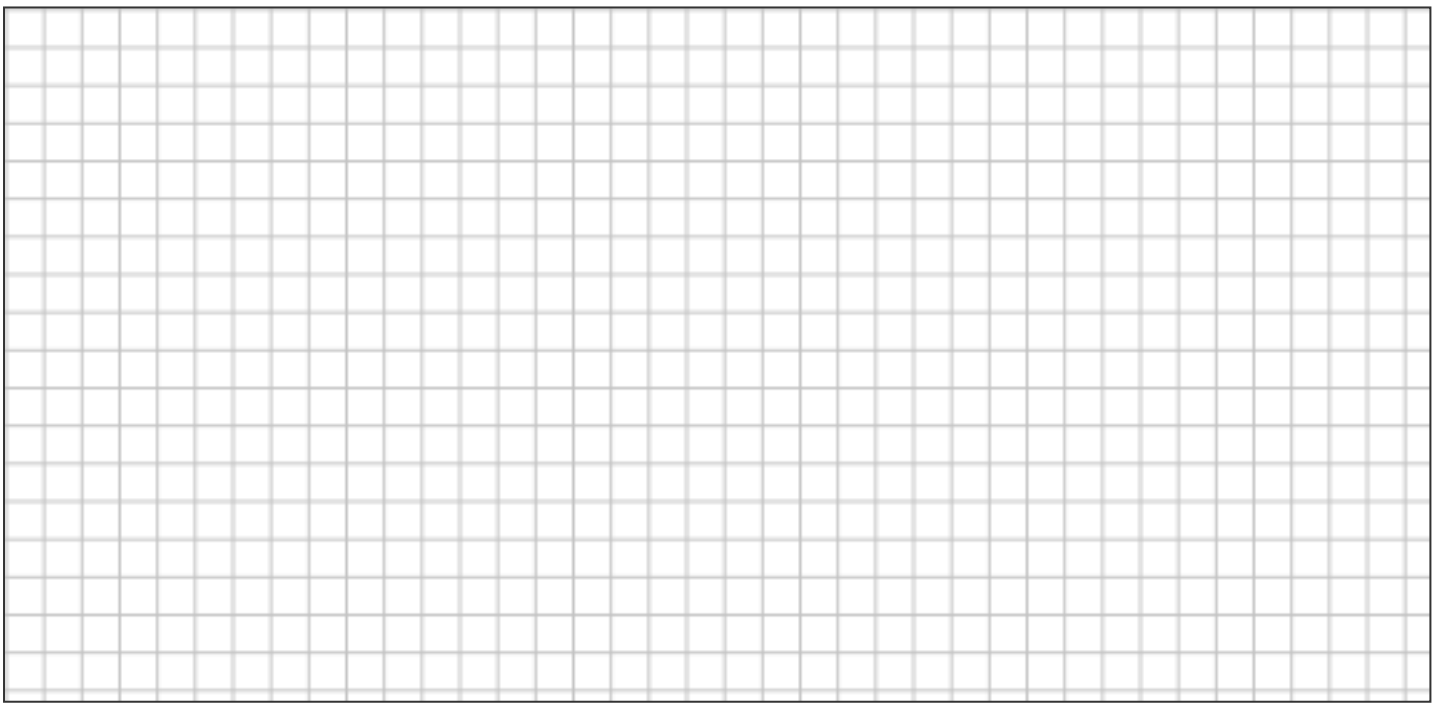

Замерщик _____ Заказчик _____