
L

LINEA

ДИЗАЙН-ПРОЕКТ ИНТЕРЬЕРА

Квартира 68 м², элитный модерн

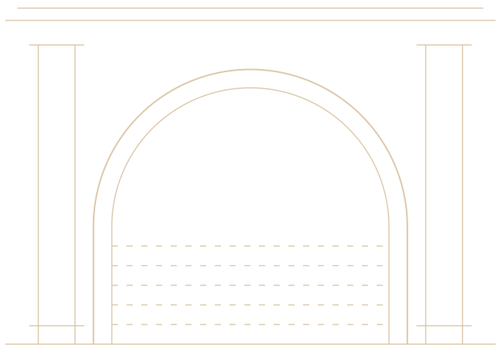

ПАЛИТРА ОТДЕЛКИ

F&B No. 2003	G503	F&B No. 34	F&B No. 281	F&B No. 43
50 %	31 %	6 %	4 %	4 %

АВТОР ПРОЕКТА

Кырлан Александр Сергеевич

Ноябрь 2026



Визуализация гостиной · 3D

ОБЩАЯ ПЛОЩАДЬ	ПОМЕЩЕНИЙ	СТАДИЯ	ШИФР	ОСНОВА
68,47 м²	7, из них жилых 3	Проект · предварительно	ГД-2026-020-АИ	план заказчика, без обмера

Как оставить правку: кнопка «Правка к этому листу» в правом верхнем углу любого листа · все листы проекта: дизайн-студия-квартир.рф/review.html?p=gost-elitemodern

выпуск 13.11.2026 № c38d47cb31 · стр. 1 из 94

Объект

Квартира 68 м², элитный модерн: 68,47 м², помещений 7, из них жилых 3.

Стиль: современный (контемпорари) 60 %, тихая роскошь (quiet luxury) 40 %. Стадия: предварительный альбом без обмера, планировка по плану заказчика.

Открытых вопросов 25, конфликтов разделов 0; изменений утверждено 7, ждут подписи 1.

Розетки и выводы

56 розеток (рамок 44), 13 выводов кабеля под технику и свет, 20 групп щита — всё с высотами от чистого пола: листы 41, 42, 45.

Что решено (подписано вами)

ИЗ-1 — Решение автора: от чистого пола до плиты 2650 мм.

ИЗ-2 — Решение автора — по предложению исполнителя: кабинет у окна (бра 12), кухня-столовая с эркером (подсветка 13), гостиная, спальня (подвесы 13-А/13-Б…

ИЗ-3 — Решение автора: большее — ванная (ванна 1700 у правой стены, умывальник на тумбе 800, стиральная машина 600 × 600 с выводами и розеткой на своей группе).

и ещё 4 — на листе реестра

Предложено, ждёт подписи: ИЗ-8

Что ждёт вашего ответа

вопросов 25; блокируют заказ или работы — 8, они первыми и выделены

№	Вопрос	Варианты · что будет без ответа	Нужен ответ
К-1	Планировка принята по обводу плана заказчика, без обмера: план заказчика распознан автоматически по картинке (1 модель ИИ, масштаб — размерные цепочки), затем исправлен…	Без ответа: размеры и расстановка на листах по брифу; мебель на заказ, двери и материалы по ним не заказывать.	**до демонтажа; до заказа мебели и дверей**
К-3	Тип дома, конструкция перекрытия и несущие стены в брифе не указаны.	Без ответа: все существующие стены считаются несущими; демонтаж и штробление в них не выполняются до технического заключения.	**до демонтажных работ**
К-7	Стиль выбран заказчиком в брифе: Современный (модерн).	Без ответа: коды — предложение исполнителя; краску, ткани и фасады не закупать до выкрасов.	**до заказа мебели и материалов**
К-8	Кухня, шкафы и встроенная техника описаны характеристиками («аналог по характеристикам»): модели не выбраны, ниши под технику — по паспорту выбранной модели.	Без ответа: выводы кухонной техники — после утверждения проекта кухни; мебель на заказ не заказывать.	**до заказа мебели и материалов**
К-24	Расчётная нагрузка 10,8 кВт (по коэффициентам спроса, без подгонки) больше принятой разрешённой 10 кВт (К-6.	Без ответа: щит собран на 10 кВт, расчётная выше разрешённой; тёплый пол и кондиционеры — предложения, к монтажу не принимать до ответа по мощности.	**до начала этих работ**
К-25	Узел ввода воды принят по умолчанию (предложение): на ХВС и ГВС — кран → фильтр грубой очистки → счётчик → обратный клапан → редуктор давления → кран с электроприводом (защита…	Без ответа: узел ввода, коллектор и электрокраны — предложение, место на листах условное; трубы и арматуру не закупать, штробы и закладные в стяжке не делать до обмера и решения.	**до заказа мебели и материалов**
К-27	Унитаз подвесной С-01 (пом. 2 «Санузел»), выпуск К1-1 Ø110: выпуск Ø110 на высоте 220 мм в инсталляции.	Варианты: (а) короб 170×140 над чистым полом вдоль стен до Ст К1-1 (1,26 м): плитка обходит короб, у двери короб не проходит; (б) подиум или подъём пола на 120 мм — ступень и порог у входа, высота двери в свету и…	**до начала этих работ**
К-28	Ванна С-04 (пом. 3 «Ванная»), выпуск К1-3 Ø50: в полу не помещается: врезка + перепад 62 (2,06 м × 30 мм/м) + Ø50 + слой над трубой 45 = 187 мм при пироге 90 мм.	Варианты: (а) короб 150×110 над чистым полом вдоль стен до Ст К1-1 (2,06 м): плитка обходит короб, у двери короб не проходит; (б) подиум или подъём пола на 100 мм — ступень и порог у входа, высота двери в свету и…	**до начала этих работ**
К-4	Стояки: на плане потолков есть только знак ⌀ в верхнем левом углу ванной (120 мм от стены) — принят за стояк канализации К1 Ø110.	Варианты значения знака: стояк / вентканал / вытяжка. Без ответа: стояки К1, В1, Т3 в коробе в углу ванной; трассы и уклоны — от них, к монтажу после обмера.	до разводки
К-5	Вентканалы в брифе не показаны: приняты у санузла и кухни.	Без ответа: вытяжка кухни — рециркуляционная; вентилятор санузла — по месту канала после обмера.	до потолков
К-6	Разрешённая мощность по ТУ в брифе не указана.	Без ответа: щит и группы рассчитаны на 10 кВт, электроплита, TN-C-S; при других ТУ — пересчёт групп варочной панели и духового шкафа, при газе — задание газовику, при TN-C — проект заземления.	до сборки щита
К-9	Состав семьи в брифе не указан (answers.household пуст): принято 2 человека.	Без ответа: расстановка и расчёты — на 2 человека.	до выпуска рабочей документации
К-10	Заказчик указал в брифе, что плана нет и нужен обмер: все размеры альбома до обмера — допущение.	Без ответа: альбом не выдаётся к работам до обмера.	до планировочного решения
К-14	Эркер кухни образмерен частично: окно 1300 мм, глубина ≈ 570 мм, скос к нижней стене ≈ 45° (на листе не образмерен, по рисунку ≈ 1150 мм, вероятно, тоже остеклён).	Без ответа: эркер — ступенькой, окно только на прямой грани; ниша штор по эркеру — по плану потолков (250 мм).	до выпуска рабочей документации
К-15	В верхней (наружной?) стене кухни на плане два узких разрыва ≈ 130 мм (над лентой 13) с участком стены 650 мм между ними.	Без ответа: не учитываются; кухонный гарнитур вдоль верхней стены — до проверки на месте.	до выпуска рабочей документации
К-16	Входная дверь на плане не помечена (марки Д-1…Д-5 — межкомнатные).	Без ответа: вход — там; входной блок — по замеру проёма.	до выпуска рабочей документации
К-17	Проём из прихожей в спальню (880 мм) без марки Д — это проём без двери или дверь, не попавшая в ведомость Д? Варианты: (1) дверь 800 с полотном, как остальные.	Проём из прихожей в спальню (880 мм) без марки Д — это проём без двери или дверь, не попавшая в ведомость Д? Варианты: (1) дверь 800 с полотном, как остальные; (2) открытый проём. Без ответа: дверь 800 × 2100 с…	до выпуска рабочей документации
К-18	В правом верхнем углу спальни прямоугольник ≈ 1300 × 290 мм вне контура потолка (без подписи): короб, шахта, пилон или шкаф.	Без ответа: участок вне помещения, мебель к нему не ставится.	до выпуска рабочей документации
К-19	У левой стены кухни рядом с Д-4 на плане синий участок «залізобетон» ≈ 640 × 90 мм (выступ стены, ригель или колонна?).	Без ответа: не учитывается до обмера.	до выпуска рабочей документации
К-20	Светильники перенесены с исходного плана: марки 01-А, 01-Б, 02, 03, 04, 05, 06-А, 06-Б, 08-А, 08-Б, 09, 10, 12 (бра), 13 (подсветка рабочей поверхности), 13-А, 13-Б, 14 и…	Без ответа: светильники по марке плана с параметрами-допущениями; закупать только после ведомости.	до заказа мебели и материалов
К-21	Ниша в прихожей «покрасить в чорний (темно-сірий)» — кода цвета нет.	Варианты: RAL 9005 (чёрный) / RAL 7016 / NCS S 8500-N. Без ответа: RAL 7016 глубокоматовая; выкрас до покраски.	до выпуска рабочей документации
К-22	Сверка с ведомостью отделки потолка заказчика: по альбому ГКЛ 61,14 м² (в ведомости 60,14), ГКЛ влагостойкий 5,81 (3,83 — санузел + ванная по размерам больше), шпаклёвка…	Без ответа: объёмы — по чертежу альбома; перед закупкой — по обмеру.	до заказа мебели и материалов
К-23	Бюджет в брифе не указан («элитный проект, премиальные материалы» — уровень, не сумма).	Без ответа: материалы премиум-уровня стиля; сумма — для согласования, не обязательство.	до выпуска рабочей документации
К-26	Климатический подрайон (СП 131.13330) не задан: принят не северный — жилые комнаты и кухня под потолком от 2,5 м (СП 54, п. 5.12).	Без ответа: отметки потолков жилых — по 2,5 м; при северном подрайоне уровни ниже 2,7 м пересчитать до заказа каркаса.	до заказа каркаса потолков
К-29	Циркуляция ГВС в данных не задана — циркуляционного трубопровода на схеме нет.	Без ответа: циркуляции на схеме нет.	до выпуска рабочей документации

Полный текст каждого вопроса, варианты и рекомендация — на листах 72, 73, 74 реестра открытых вопросов.

	Лист	№ док.	Подпись	Дата	Проект: Квартира 68 м², элитный модерн			
Дизайнер	Кырлан А.С.			13.11.26	Ваш проект на одной странице	Стадия	Лист	Листов
Проверил						П	2	94
Н. контр.								
Утв.								



	Лист	№ док.	Подпись	Дата	Проект: Квартира 68 м², элитный модерн			
Дизайнер	Кырлан А.С.			13.11.26				
Проверил					Визуализация кабинета	Стадия	Лист	Листов
Н. контр.								
Утв.						П	3	94

выпуск 13.11.2026 № c38d47cb31 · стр. 3 из 94



	Лист	№ док.	Подпись	Дата	Проект: Квартира 68 м², элитный модерн			
Дизайнер	Кырлан А.С.			13.11.26	Визуализация санузла	Стадия	Лист	Листов
Проверил						П	4	94
Н. контр.								
Утв.								



	Лист	№ док.	Подпись	Дата
Дизайнер	Кырлан А.С.			13.11.26
Проверил				
Н. контр.				
Утв.				

Проект: Квартира 68 м², элитный модерн

Визуализация ванной	Стадия	Лист	Листов
	П	5	94



	Лист	№ док.	Подпись	Дата	Проект: Квартира 68 м², элитный модерн			
Дизайнер	Кырлан А.С.			13.11.26				
Проверил					Визуализация ванной	Стадия	Лист	Листов
Н. контр.								
Утв.						П	6	94

выпуск 13.11.2026 № c38d47cb31 · стр. 6 из 94



	Лист	№ док.	Подпись	Дата
Дизайнер	Кырлан А.С.			13.11.26
Проверил				
Н. контр.				
Утв.				

Проект: Квартира 68 м², элитный модерн

Визуализация ванной	Стадия	Лист	Листов
	П	7	94



	Лист	№ док.	Подпись	Дата	Проект: Квартира 68 м², элитный модерн			
Дизайнер	Кырлан А.С.			13.11.26				
Проверил					Визуализация прихожей	Стадия	Лист	Листов
Н. контр.						П	8	94
Утв.								



	Лист	№ док.	Подпись	Дата	Проект: Квартира 68 м², элитный модерн			
Дизайнер	Кырлан А.С.			13.11.26				
Проверил					Визуализация гостиной	Стадия	Лист	Листов
Н. контр.						П	9	94
Утв.								

выпуск 13.11.2026 № c38d47cb31 · стр. 9 из 94



	Лист	№ док.	Подпись	Дата	Проект: Квартира 68 м², элитный модерн			
Дизайнер	Кырлан А.С.			13.11.26				
Проверил					Визуализация гостиной	Стадия	Лист	Листов
Н. контр.								
Утв.						П	10	94

выпуск 13.11.2026 № c38d47cb31 · стр. 10 из 94



	Лист	№ док.	Подпись	Дата	Проект: Квартира 68 м², элитный модерн			
Дизайнер	Кырлан А.С.			13.11.26				
Проверил					Визуализация спальни	Стадия	Лист	Листов
Н. контр.								
Утв.						П	11	94

выпуск 13.11.2026 № c38d47cb31 · стр. 11 из 94

Список листов

Лист	Наименование
1	Титульный лист
2	Ваш проект на одной странице
3	Визуализация кабинета
4	Визуализация санузла
5	Визуализация ванной
6	Визуализация ванной
7	Визуализация ванной
8	Визуализация прихожей
9	Визуализация гостиной
10	Визуализация гостиной
11	Визуализация спальни
12	Список листов
13	Как читать альбом
14	План планировки от заказчика
15	План монтажный
16	Кухня (пом. 5). Монтажная схема
17	Шкафы. Монтажная схема
18	Карта покрытий стен
19	Колерная карта
20	План размещения мебели и оборудования
21	Спецификация мебели и оборудования
22	Спецификация мебели и оборудования (продолжение)
23	Спецификация мебели и оборудования (продолжение)
24	Спецификация мебели и оборудования (продолжение)
25	Ведомости изделий, техники и фурнитуры
26	План выводов сантехники
27	Схема разводки водопровода и канализации
28	Аксонометрическая схема В1 (холодное водоснабжение)
29	Аксонометрическая схема Т3 (горячее водоснабжение)
30	Аксонометрическая схема К1 (канализация)
31	Развёртки мокрых зон: выводы ВК. Санузел
32	Развёртки мокрых зон: выводы ВК. Ванная
33	Развёртки мокрых зон: выводы ВК. Кухня-столовая
34	Спецификация сантехнического оборудования
35	Раскладка плитки. Санузел. Развёртки стен
36	Раскладка плитки. Ванная. Развёртки стен
37	План размещения дверей
38	План потолков
39	Разрезы и узлы потолков
40	Сечения потолков М 1:10

Лист	Наименование
41	Однолинейная схема щита
42	Однолинейная схема щита (продолжение)
43	Таблица нагрузок щита
44	План принципиальных трасс
45	План розеток и электровыводов
46	План слаботочных сетей
47	План освещения
48	Техническое задание на подбор светильников
49	Управление светильниками
50	План вентиляции
51	План отопления
52	План покрытий пола
53	Раскладка плитки. Планы полов
54	Раскладка плитки. Фартук кухни
55	Развёртки стен А, Б. Кабинет (пом. 1)
56	Развёртки стен В, Г. Кабинет (пом. 1)
57	Развёртки стен А, Б. Санузел (пом. 2)
58	Развёртки стен В, Г. Санузел (пом. 2)
59	Развёртки стен А, Б. Ванная (пом. 3)
60	Развёртки стен В, Г. Ванная (пом. 3)
61	Развёртки стен А, Б. Прихожая (пом. 4)
62	Развёртки стен В, Г. Прихожая (пом. 4)
63	Развёртка стены А1. Кухня-столовая (пом. 5), кухонный фронт
64	Развёртки стен А2, Б1, Б2. Кухня-столовая (пом. 5)
65	Развёртки стен В, Г. Кухня-столовая (пом. 5)
66	Развёртки стен А, Б. Гостиная (пом. 6)
67	Развёртки стен В, Г. Гостиная (пом. 6)
68	Развёртка стены А1. Спальня (пом. 7)
69	Развёртки стен А2, Б. Спальня (пом. 7)
70	Развёртка стены В. Спальня (пом. 7)
71	Развёртка стены Г. Спальня (пом. 7)
72	Открытые вопросы, принятые допущения и конфликты. Лист 1 из 3
73	Открытые вопросы, принятые допущения и конфликты. Лист 2 из 3
74	Открытые вопросы, принятые допущения и конфликты. Лист 3 из 3
Д1	Шкаф-купе М-04
Д2	Кухня (пом. 5). Развёртка гарнитура

Лист	Наименование
С1	Ведомость отделки помещений. Лист 1 из 2
С2	Ведомость отделки помещений. Лист 2 из 2
С3	Спецификация отделочных материалов
С4	Список покупок
С5	Список покупок (окончание)
С6	Смета проекта: этапы, помещения, итог
С7	Смета проекта: этапы, помещения, итог (продолжение)
С8	Смета проекта: этапы, помещения, итог (окончание)
С9	Смета материалов с ценами
С10	Смета материалов с ценами (продолжение)
С11	Смета материалов с ценами (продолжение)
С12	Смета материалов с ценами (окончание)
С13	Узлы
С14	Календарный график работ и закупок
С15	Чек-лист приёмки по этапам. Лист 1 из 3
С16	Чек-лист приёмки по этапам. Лист 2 из 3
С17	Чек-лист приёмки по этапам. Лист 3 из 3
С18	Лист → мастер

1. Размеры даны в мм от чистовых поверхностей стен: слой штукатурки 20 мм по блоку и 5 мм шпаклёвки по ГКЛ учтён. Перед заказом встроенной мебели — контрольный обмер после штукатурки.
2. Привязки мебели — от стен и углов помещения, а не от другой мебели.
3. Розетки, выводы и выключатели под мебель — см. лист 45 «План розеток и электровыводов»; сантехприборы и выводы воды — лист 26.
4. План расстановки не является документацией для изготовления мебели: изделия — по чертежам мебельщика; покупную мебель заменять только на изделия не больше габарита из спецификации (лист 21).
5. Встроенная мебель «стена в стену» — с зазором 10 мм с каждой стороны или с компенсаторами.
6. Развёртки — вид на стену изнутри помещения, по часовой стрелке; расположение стен на схеме листа развёртки; размеры — в мм по чистовым поверхностям; отметки — в м от ±0,000; высоты Н — от чистого пола помещения до оси изделия, у декора — до центра.
7. Красная цепочка — привязки электроточек и выводов по осям от угла чистовых стен; высота Н — у знака, от чистого пола до оси; высоты мебели, проёмов и границ отделки колонкой отметок слева. У знака — короткая марка; назначение, группа щита, высота и привязка каждой точки и вывода — в «Ведомости точек и выводов» под видами (каждая точка — строка).
8. У знака электроточки: марка (Р — розетка, S — выключатель, Св — светильник, ЭВ вывод кабеля), ×N — число постов в рамке, гр. — группа щита, Н — высота оси от чистого пола, мм; группы по клавишам выключателя — на листе выключателей.
9. Схема мебели, приборов и декора не является технической документацией для производства мебели; габариты — по паспортам изделий.
10. Марки позиций: М-NN — мебель, ОБ-NN — оборудование, С-NN — сантехника; О-N отделка (ведомость отделочных материалов, серия С).
11. Размеры мебели и изделий на заказ уточнить по месту после отделочных работ.

	Лист	№ док.	Подпись	Дата	Проект: Квартира 68 м², элитный модерн			
Дизайнер	Кырлан А.С.			13.11.26				
Проверил					Список листов	Стадия	Лист	Листов
Н. контр.								
Утв.						П	12	94

выпуск 13.11.2026 № c38d47cb31 · стр. 12 из 94

Общие указания

Что в альбоме

Альбом — дизайн-проект с рабочими чертежами для ремонта. Листы идут в порядке работ: титул и вводные, реестр открытых вопросов и решений, планы (обмер, монтаж стен, мебель, двери, потолки, полы), инженерия (сантехника, электрика, вентиляция и отопление), развёртки стен с визуализациями помещений, чертежи мебели, ведомости материалов и узлы.

Вам как заказчику — титул, эта вводная, «Ваш проект на одной странице», реестр вопросов, план мебели, визуализации и развёртки, ведомости мебели и материалов. Подрядчику — всё остальное: монтажные планы, привязки выводов и розеток, узлы, ведомости объёмов.

Знаки на листах

Без знака — решение утверждено или подтверждено обмером.

Что проверить до ремонта

1. Розетки у кровати и рабочего места: хватает ли их с каждой стороны кровати и над столом (план розеток — лист 45).

2. Выводы под технику — варочная панель, духовка, посудомойка, стиральная машина, бойлер: совпадают ли с выбранными моделями (листы 21, 22, 23, 24, 45).

3. Высоты розеток, выключателей и выводов даны от чистого пола: если мебель или техника будут другими — скажите до штробления стен.

Номера записей

К-N — открытый вопрос: чего не хватает или что выбрать (варианты и рекомендация — в тексте). Пока ответа нет, действует строка «если решения нет».

Кф-N — конфликт между разделами (например, мебель и радиатор в одном месте); закрывается решением, которое записывается как ИЗ-N.

ИЗ-N — изменение проекта: что было, что стало и кто утвердил. Изменение без подписи предложение.

Все записи — на листе реестра сразу после вводных; на других листах на них стоят ссылки.

Почему альбом предварительный

Обмера на объекте не было: размеры взяты с плана заказчика. Технические условия (мощность, вода, вентиляция дома) не получены, часть решений ждёт вашего ответа. Пока в реестре есть открытые вопросы, альбом предварительный — пометка в штампе снимается закрытием вопросов, а не стиранием.


Правку к любому листу можно оставить по кнопке «Правка к листу» или на сайте студии: дизайн-студия-квартир.рф — укажите номер листа и что изменить.

3 круга правок входят в цену; условия — в договоре и на странице вашего заказа на сайте студии.

Шифр проекта ГД-2026-020-АИ

	Лист	№ док.	Подпись	Дата	Проект: Квартира 68 м², элитный модерн			
Дизайнер	Кырлан А.С.			13.11.26	Как читать альбом	Стадия	Лист	Листов
Проверил						П	13	94
Н. контр.								
Утв.								

выпуск 13.11.2026 № c38d47cb31 · стр. 13 из 94

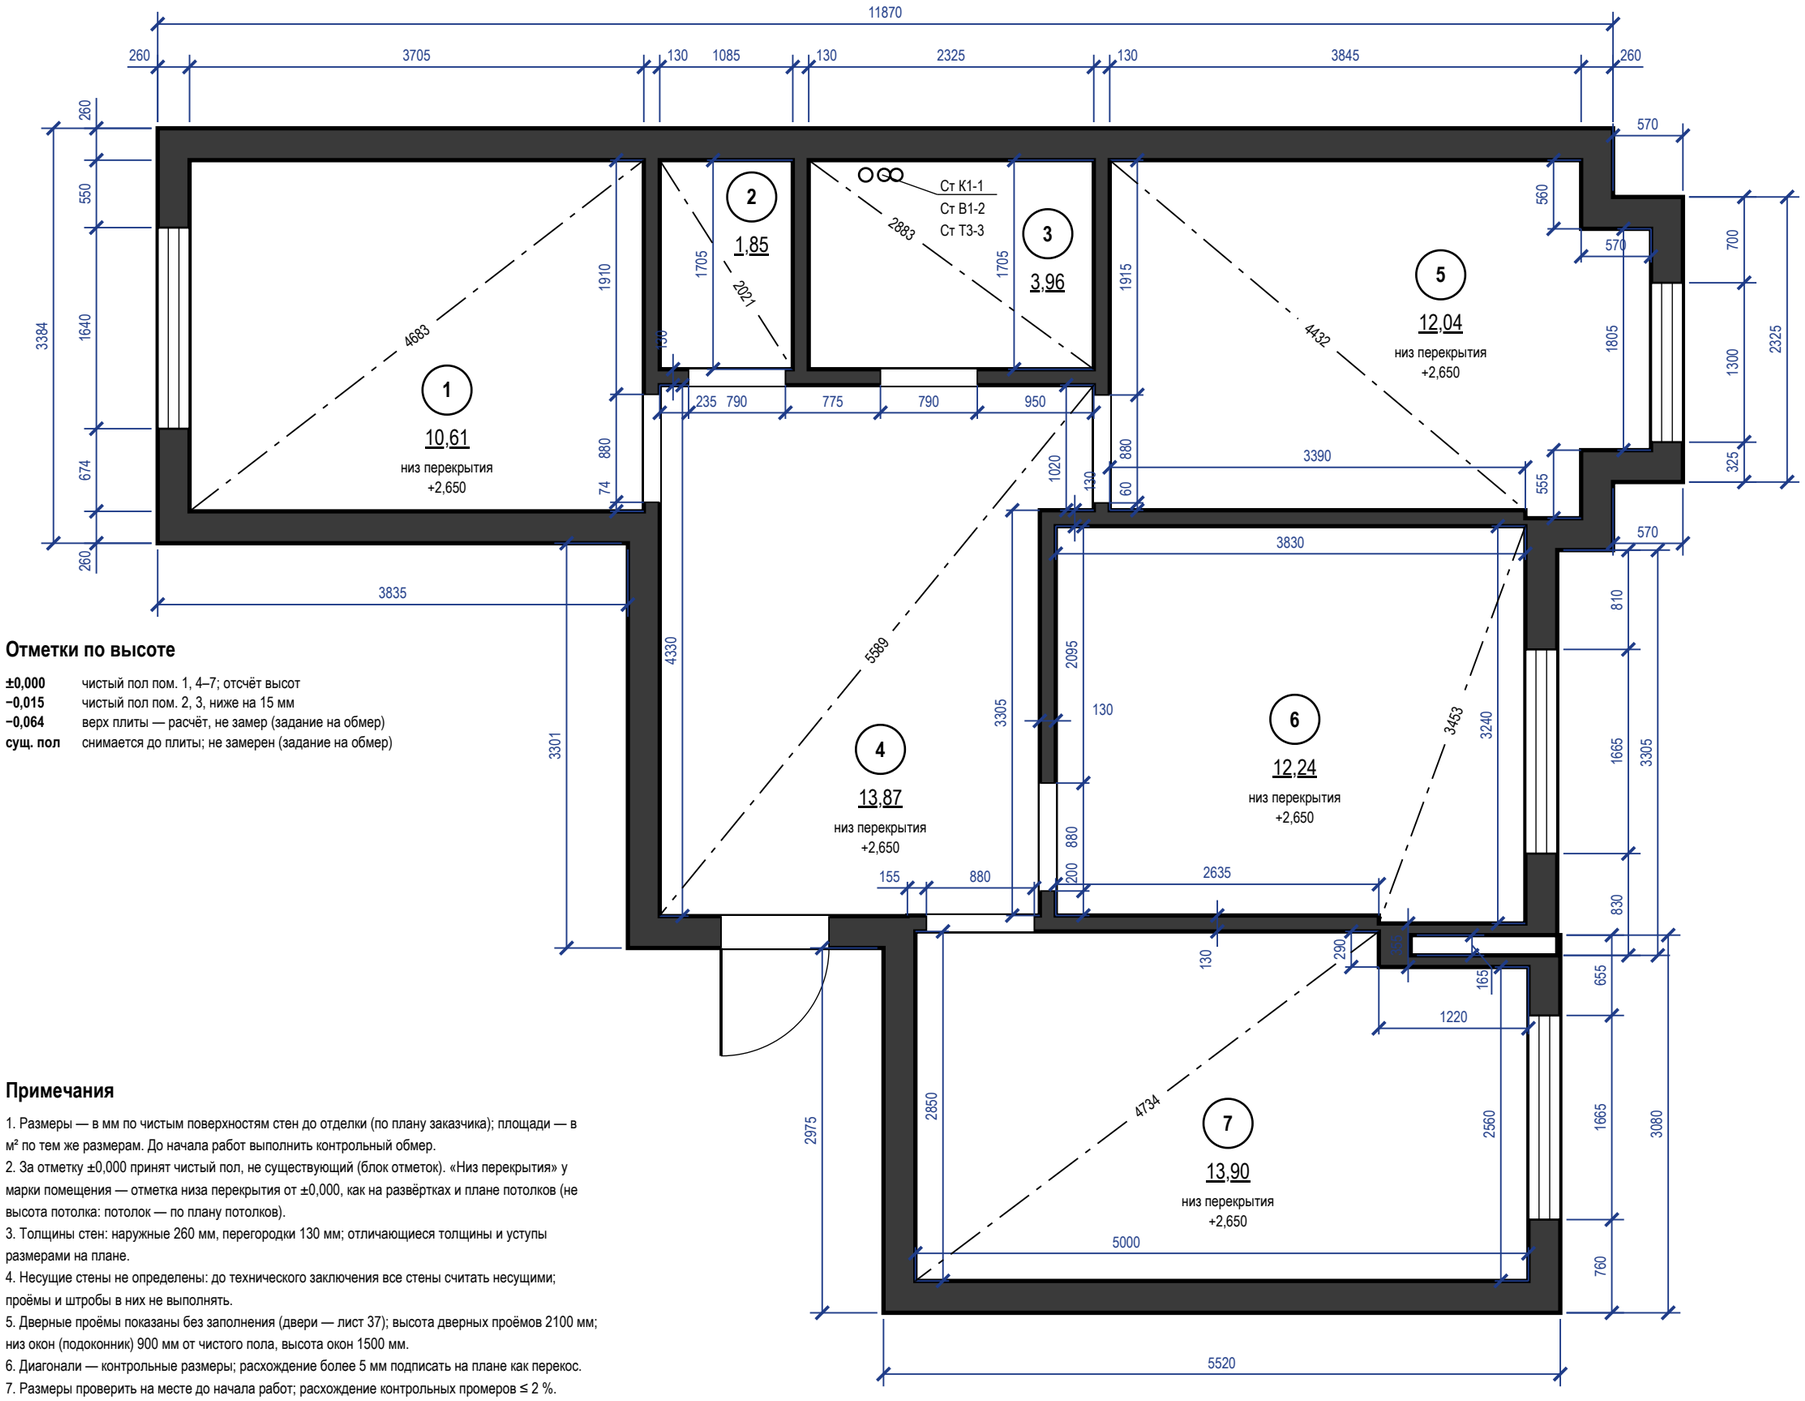

Экспликация помещений

№	Наименование	Площадь, м²
1	Кабинет	10,61
2	Санузел	1,85
3	Ванная	3,96
4	Прихожая	13,87
5	Кухня-столовая	12,04
6	Гостиная	12,24
7	Спальня	13,90
	Итого (общая площадь)	**68,47**

Условные обозначения

- существующие стены (сечение)
- окно (рама, остекление)
- проём существующий, без заполнения (откосы)
- стояк: К1 — канализация, В1 — ХВС, Т3 — ГВС
- диагональ помещения — контроль прямоугольности
- (1) номер помещения, площадь м²

Отметки по высоте


±0,000	чистый пол пом. 1, 4–7; отсчёт высот
−0,015	чистый пол пом. 2, 3, ниже на 15 мм
−0,064	верх плиты — расчёт, не замер (задание на обмер)
сущ. пол	снимается до плиты; не замерен (задание на обмер)

Примечания

1. Размеры — в мм по чистым поверхностям стен до отделки (по плану заказчика); площади — в м² по тем же размерам. До начала работ выполнить контрольный обмер.
2. За отметку ±0,000 принят чистый пол, не существующий (блок отметок). «Низ перекрытия» у марки помещения — отметка низа перекрытия от ±0,000, как на развёртках и плане потолков (не высота потолка: потолок — по плану потолков).
3. Толщины стен: наружные 260 мм, перегородки 130 мм; отличающиеся толщины и уступы размерами на плане.
4. Несущие стены не определены: до технического заключения все стены считать несущими; проёмы и штробы в них не выполнять.
5. Дверные проёмы показаны без заполнения (двери — лист 37); высота дверных проёмов 2100 мм; низ окон (подоконник) 900 мм от чистого пола, высота окон 1500 мм.
6. Диагонали — контрольные размеры; расхождение более 5 мм подписать на плане как перекос.
7. Размеры проверить на месте до начала работ; расхождение контрольных промеров ≤ 2 %.
8. Размеры короче 1 мм на листе цепочкой не показаны (две выносные линии на таком расстоянии сливаются): пом. 4, стена В — 45 мм от проёма до угла.

	Лист	№ док.	Подпись	Дата	Проект: Квартира 68 м², элитный модерн			М 1:50
Дизайнер	Кырлан А.С.			13.11.26				
Проверил					План планировки от заказчика	Стадия	Лист	Листов
Н. контр.						П	14	94
Утв.								

выпуск 13.11.2026 № c38d47cb31 · стр. 14 из 94

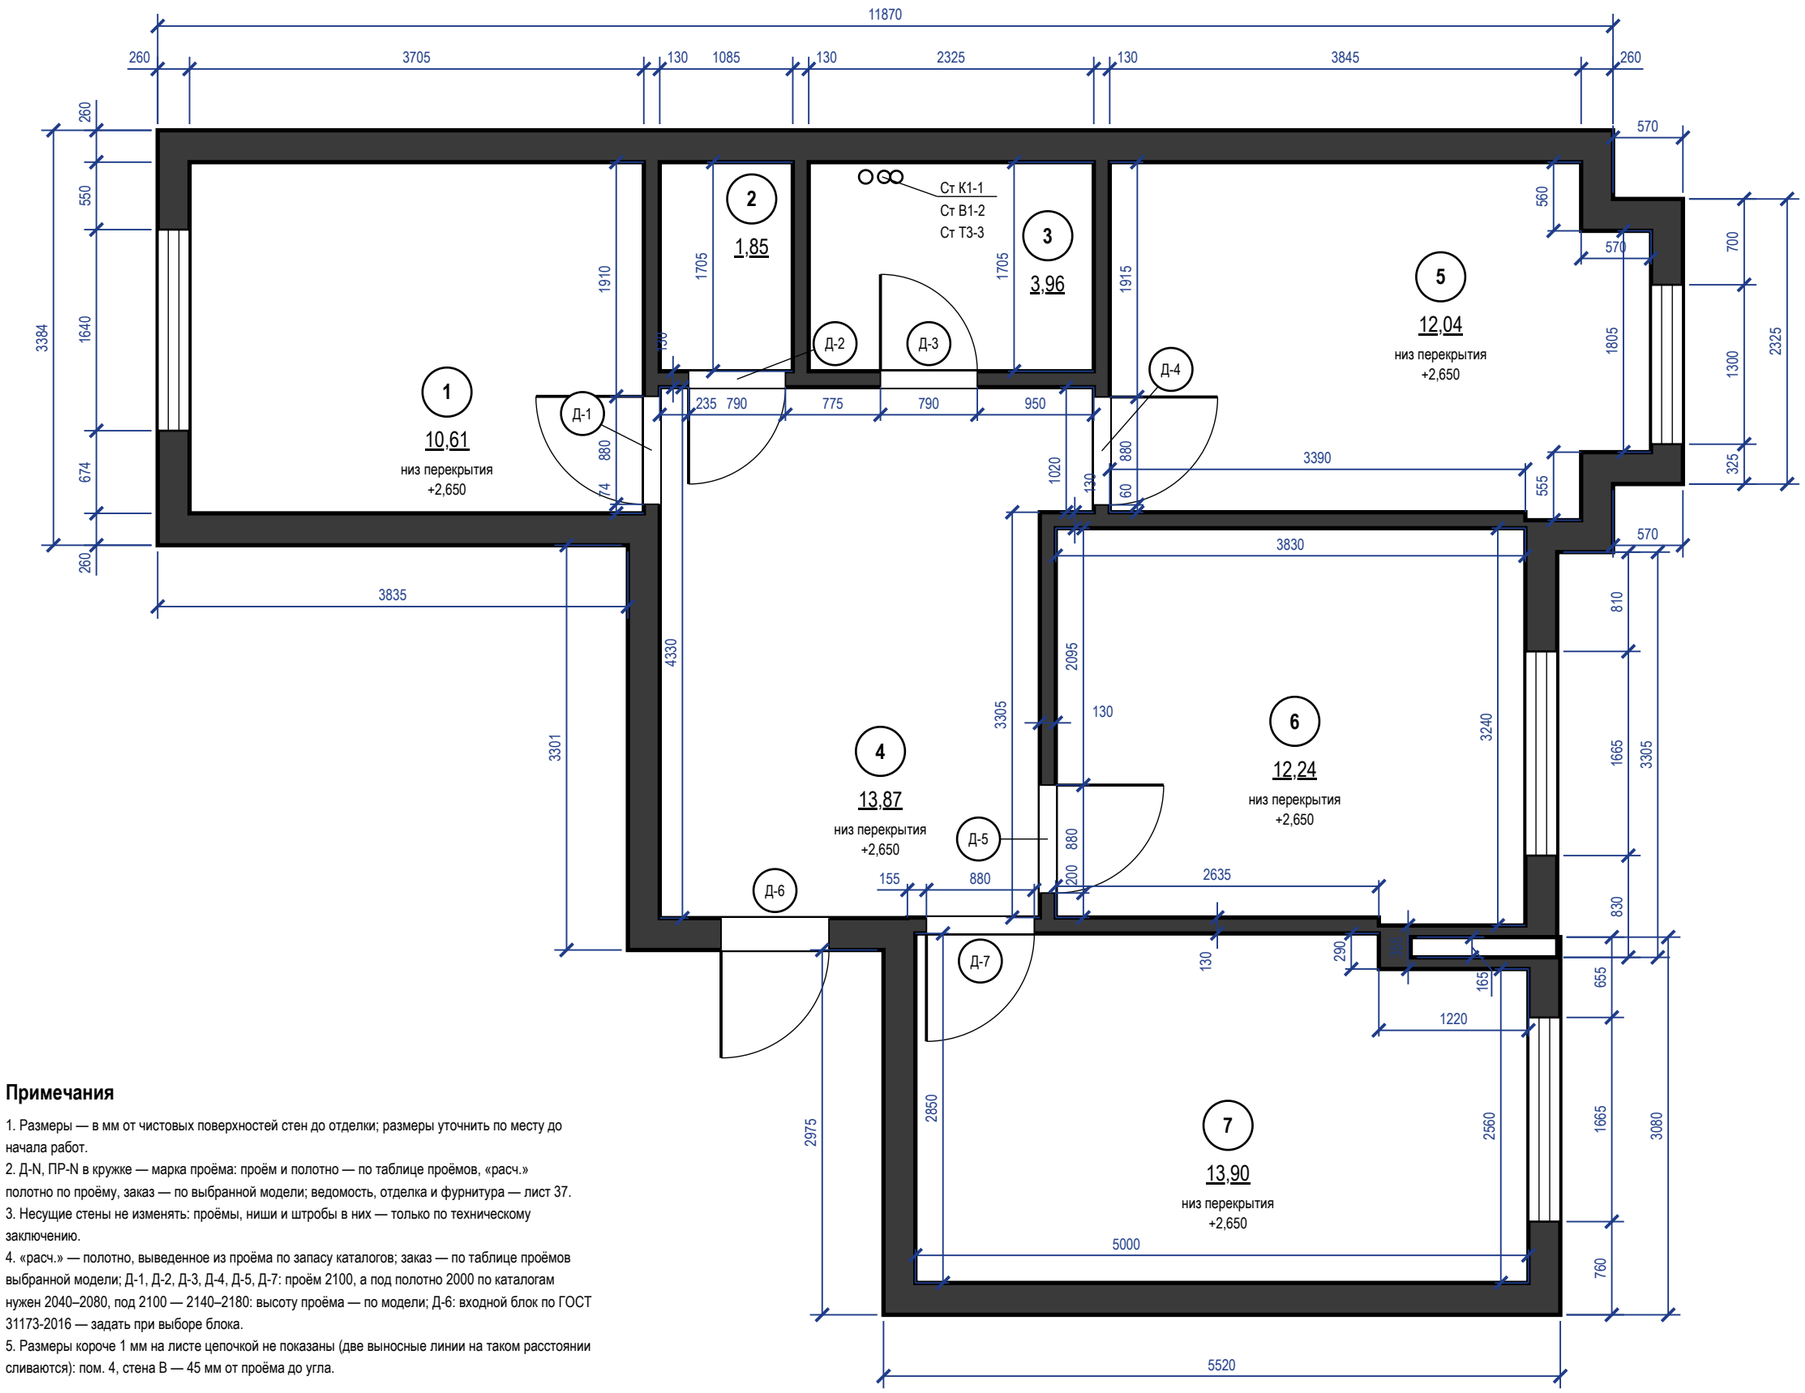

Экспликация помещений

№	Наименование	Площадь, м²
1	Кабинет	10,61
2	Санузел	1,85
3	Ванная	3,96
4	Прихожая	13,87
5	Кухня-столовая	12,04
6	Гостиная	12,24
7	Спальня	13,90
	Итого (общая площадь)	**68,47**

Таблица проёмов

Марка	Наименование	Проём ш×в, мм	Полотно (расч.)
Д-1	Дверь распашная	880×2100	800×2000
Д-2	Дверь распашная	790×2100	700×2000
Д-3	Дверь распашная	790×2100	700×2000
Д-4	Дверь распашная	880×2100	800×2000
Д-5	Дверь распашная	880×2100	800×2000
Д-6	Дверь входная	880×2100	блок — задать
Д-7	Дверь распашная	880×2100	800×2000

Примечания

1. Размеры — в мм от чистовых поверхностей стен до отделки; размеры уточнить по месту до начала работ.
2. Д-N, ПР-N в кружке — марка проёма: проём и полотно — по таблице проёмов, «расч.» полотно по проёму, заказ — по выбранной модели; ведомость, отделка и фурнитура — лист 37.
3. Несущие стены не изменять: проёмы, ниши и штробы в них — только по техническому заключению.
4. «расч.» — полотно, выведенное из проёма по запасу каталогов; заказ — по таблице проёмов выбранной модели; Д-1, Д-2, Д-3, Д-4, Д-5, Д-7: проём 2100, а под полотно 2000 по каталогам нужен 2040–2080, под 2100 — 2140–2180: высоту проёма — по модели; Д-6: входной блок по ГОСТ 31173-2016 — задать при выборе блока.
5. Размеры короче 1 мм на листе цепочкой не показаны (две выносные линии на таком расстоянии сливаются): пом. 4, стена В — 45 мм от проёма до угла.

	Лист	№ док.	Подпись	Дата
Дизайнер	Кырлан А.С.			13.11.26
Проверил				
Н. контр.				
Утв.				


Проект: Квартира 68 м², элитный модерн — **М 1:50**

План монтажный


Стадия	Лист	Листов
П	15	94

выпуск 13.11.2026 № c38d47cb31 · стр. 15 из 94

Привязка выводов и крепление модулей (М 1:25)

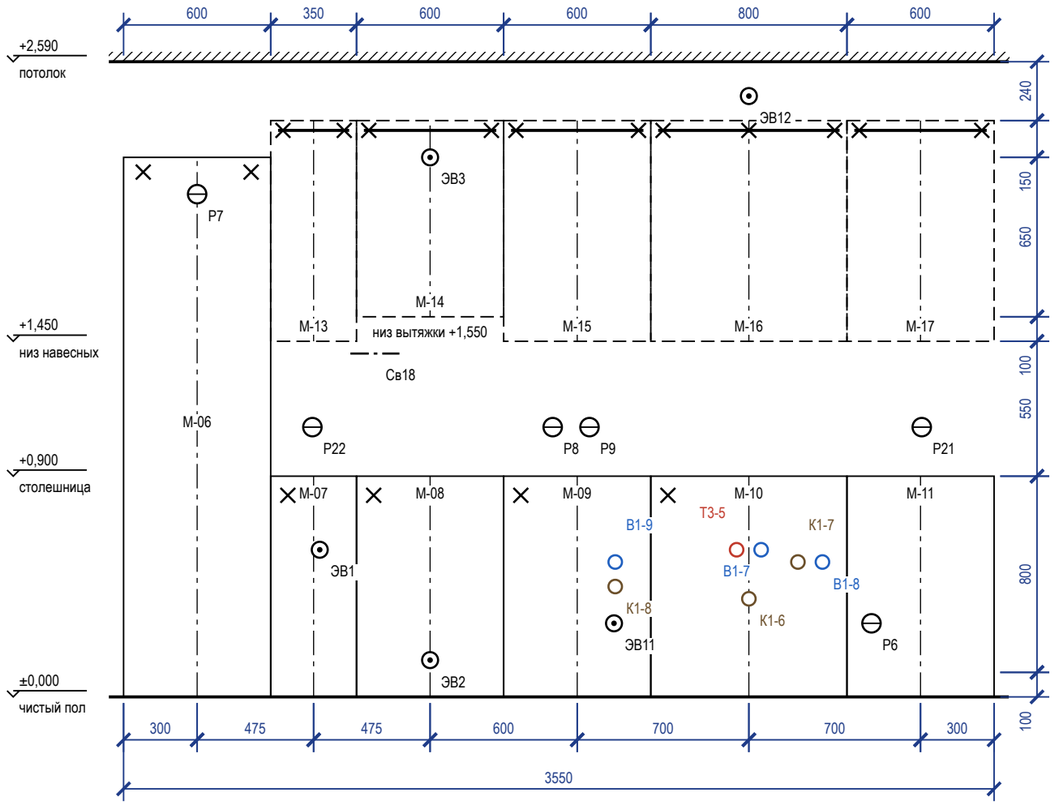

План столешницы (М 1:25)

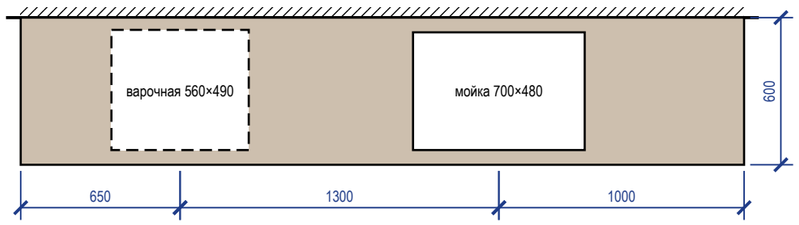

Примечания

1. Выводы — по проекту электрики и ВК; привязка по горизонтали — от оси модуля (плюс — вправо по виду), по высоте — от чистого пола до оси вывода.
2. Пенал — уголки к стене 2 шт. сверху; нижние модули — стяжками между собой и уголком к стене; ряд выставить по уровню опорами цоколя.
3. Розетки над столешницей — не ниже 150 мм над ней и не за корпусом техники; розетка за ПММ, духовым шкафом и холодильником — только в соседнем модуле или в зоне цоколя с доступом.
4. Столешница — вырезы по шаблонам выбранных моделей мойки и варочной панели; торцы у стены — герметик, пристеночный плинтус.

Условные обозначения

- нижний модуль, пенал (контур)
- невидимый контур: навесной модуль, корпус под столешницей
- ось модуля (от неё — привязка вывода)
- анкер / уголок крепления к стене
- розетка на стене
- вывод кабеля к технике
- B1 — вывод воды В1 / Т3, канализации К1

Привязка выводов к осям модулей

Код	Назначение	Модуль	От оси, мм	Н, мм	Размещение
Р7	розетка — холодильник — над нишей, съёмная панель	М-06	0	2050	над нишей холодильника, съёмная панель
Р22	розетка ×2 — фартук	М-07	−5	1100	над столешницей (фартук)
ЭВ1	вывод кабеля — варочная панель — в соседнем модуле, за ящиком	М-07	+25	600	в соседнем модуле, за ящиком
Св18	светодиодная лента — марка 13 по исходному плану: «підсвітка робочої поверхні»	М-08	−225	1400	над столешницей (фартук)
ЭВ2	вывод кабеля — духовой шкаф — в цоколе	М-08	0	150	под духовым шкафом, доступ через ящик
ЭВ3	вывод кабеля — вытяжка — над корпусом	М-14	0	2200	в навесном модуле
Р8	розетка ×2 — чайник и кофемашина (отдельная линия)	М-09	−100	1100	над столешницей (фартук)
Р9	розетка — фартук: мелкая техника	М-09	+50	1100	над столешницей (фартук)
ЭВ11	вывод кабеля — измельчитель мойки	М-09	+150	300	в соседнем модуле, за ящиком
В1-9	В1 — ro-filter	М-09	+155	550	в соседнем модуле, за ящиком
К1-8	К1 Ø40 — ro-filter	М-09	+155	450	в соседнем модуле, за ящиком
Т3-5	Т3 — межос. 100	М-10	−50	600	в модуле мойки
ЭВ12	вывод кабеля — подсветка навесных шкафов (блок питания ленты)	М-16	0	2450	в навесном модуле
К1-6	К1 Ø50 — мойка	М-10	0	400	в модуле мойки
В1-7	В1 — межос. 100	М-10	+50	600	в модуле мойки
К1-7	К1 Ø40 — слив ПММ в шкафу мойки	М-10	+200	550	в модуле мойки
В1-8	В1 — кран ПММ в шкафу мойки	М-10	+300	550	в модуле мойки
Р6	розетка — посудомоечная машина (в нише М-11, сбоку от корпуса, доступ через цоколь)	М-11	−200	300	за ПММ — перенести в соседний модуль
Р21	розетка ×2 — фартук	М-11	+5	1100	над столешницей (фартук)


Зазоры под отделку

Поверхность	Отделка	Зазор, мм	Учесть
фартук	керамогранит	10	от чернового основания до корпуса навесных и столешницы
стены	окраска	5	под штукатурку и шпаклёвку за пеналом
пол	инженерная доска		цоколь — после укладки пола, опоры ±20 мм

	Лист	№ док.	Подпись	Дата	Проект: Квартира 68 м², элитный модерн			М 1:25
Дизайнер	Кырлан А.С.			13.11.26	Кухня (пом. 5). Монтажная схема	Стадия	Лист	Листов
Проверил						П	16	94
Н. контр.								
Утв.								

выпуск 13.11.2026 № c38d47cb31 · стр. 16 из 94

Шкаф-купе М-04 (пом. 4) (М 1:25)

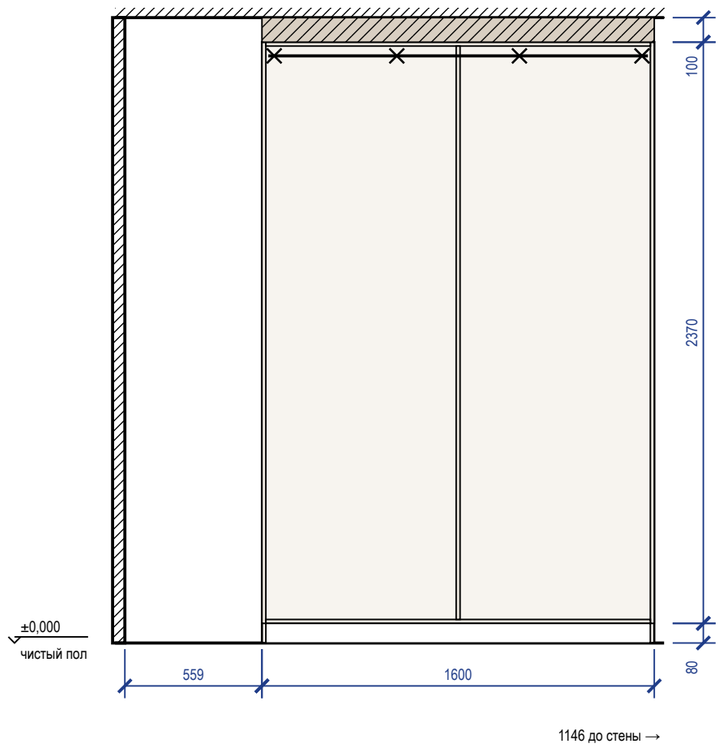

Крепление и зазоры под отделку

Марка	Помещение, стена	Основание	Отделка стены	Зазор, мм	Крепёж по планке	От опрокидывания
М-04	Прихожая (4), стена Б	по основанию — см. таблицу крепежа	окраска	5	анкер 4 шт., шаг 500	уголки 2 шт.

Крепёж по основанию стены

Основание стены	Крепёж
бетон, ж/б	анкер-шуруп 7,5×72 или дюбель 8×60 с шурупом 5×70
кирпич полнотелый	дюбель 8×80 с шурупом 5×90
газобетон, пазогребень	дюбель для газобетона 10×100 или химический анкер
гипсокартон	закладная до обшивки (брус 40×80 или фанера 18 мм), саморез в закладную

Условные обозначения

- анкер / уголок крепления к стене
- корпус и полки ЛДСП (вид на стену)
- компенсатор — короб до потолка

Примечания

1. Установочные размеры — от чистого пола и чистых стен; перед установкой контрольный замер после отделки.
2. Порядок: корпус выставить по уровню опорами цоколя → закрепить к стене по задней планке → навесить двери и фасады, отрегулировать зазоры → подогнать и закрепить компенсатор.
3. Анкеры — с шагом не более 500 мм, не ближе 50 мм от края планки; на ГКЛ только в закладную, установленную до обшивки.
4. Скрытые коммуникации под анкеры проверить детектором; трассы электрики по плану розеток.

	Лист	№ док.	Подпись	Дата	Проект: Квартира 68 м², элитный модерн			М 1:25
Дизайнер	Кырлан А.С.			13.11.26	Шкафы. Монтажная схема	Стадия	Лист	Листов
Проверил						П	17	94
Н. контр.								
Утв.								

выпуск 13.11.2026 № c38d47cb31 · стр. 17 из 94



Покрытия стен

Марка	Покрытие	Помещение: S, м²	Итого, м²
O1	окраска Farrow & Ball · No. 2003 «Pointing»	1: 19,9; 4: 22,4; 5: 22,3; 6: 22,1; 7: 25,7	112,5
O2	окраска Tikkurila · No. 30 «Hague Blue — глубокий сине-зелёный»	1: 9,5	9,5
O6	облицовка плиткой · 600×1200 мм	2: 11,3; 3: 17,3	28,5
O10	окраска Tikkurila · No. 281 «Stiffkey Blue — чернильный синий»	5: 9,9	9,9
O11	окраска Farrow & Ball · No. 43 «Eating Room Red — брусничный красный»	6: 9,8	9,8
O12	окраска Farrow & Ball · No. 34 «Calke Green — традиционный шалфей»	7: 10,0	10,0

Площади — нетто, по развёрткам (за вычетом проёмов и фартука); высоты помещений — от чистого пола.

	Лист	№ док.	Подпись	Дата
Дизайнер	Кырлан А.С.			13.11.26
Проверил				
Н. контр.				
Утв.				

Проект: Квартира 68 м², элитный модерн — **М 1:50**

Карта покрытий стен

Стадия	Лист	Листов
П	18	94

выпуск 13.11.2026 № c38d47cb31 · стр. 18 из 94

Колерная карта по помещениям

Помещение	Поверхность	Образец	Поз.	Система и код цвета	Производитель, линейка / материал, артикул	Блеск	Класс истирания	LRV	Площадь
1. Кабинет 10,61 м²	стены		**К1**	Farrow & Ball No. 2003	Farrow & Ball · Modern Emulsion	матовая	1	86	20,1 м²
	акцент В		**К2**	Farrow & Ball No. 30	Tikkurila · Euro Power 7, колеровка по NCS	матовая	1	7	9,6 м²
	потолок		**К3**	Tikkurila G503	Tikkurila · Euro Power 7	глубокомат.	2	89	10,6 м²
	пол		**КМ1**	по образцу	инженерная доска · аналог по хар.				10,6 м²
	плинтус		**К4**	Farrow & Ball No. 2003	МДФ · в цвет Farrow & Ball			86	12,3 м
2. Санузел 1,85 м²	стены		**КМ2**	по образцу	плитка · аналог по хар.				11,8 м²
	потолок		**К5**	Tikkurila G503	Tikkurila · Euro Power 7	матовая	1	89	1,9 м²
	пол		**КМ3**	по образцу	керамогранит · аналог по хар.				1,9 м²
3. Ванная 3,96 м²	стены		**КМ2**	по образцу	плитка · аналог по хар.				17,7 м²
	потолок		**К5**	Tikkurila G503	Tikkurila · Euro Power 7	матовая	1	89	4,0 м²
	пол		**КМ3**	по образцу	керамогранит · аналог по хар.				4,0 м²
4. Прихожая 13,87 м²	стены		**К1**	Farrow & Ball No. 2003	Farrow & Ball · Modern Emulsion	матовая	1	86	23,5 м²
	потолок		**К3**	Tikkurila G503	Tikkurila · Euro Power 7	глубокомат.	2	89	13,9 м²
	пол		**КМ4**	по образцу	керамогранит · аналог по хар.				13,9 м²
	плинтус		**К4**	Farrow & Ball No. 2003	МДФ · в цвет Farrow & Ball			86	9,8 м
5. Кухня-столовая 12,04 м²	стены		**К1**	Farrow & Ball No. 2003	Farrow & Ball · Modern Emulsion	матовая	1	86	22,6 м²
	акцент В		**К6**	Farrow & Ball No. 281	Tikkurila · Euro Power 7, колеровка по NCS	матовая	1	10.1	10,0 м²
	потолок		**К3**	Tikkurila G503	Tikkurila · Euro Power 7	глубокомат.	2	89	12,0 м²
	пол		**КМ1**	по образцу	инженерная доска · аналог по хар.				12,0 м²
	плинтус		**К4**	Farrow & Ball No. 2003	МДФ · в цвет Farrow & Ball			86	13,8 м
	фартук		**КМ5**	по образцу	керамогранит · аналог по хар.				1,7 м²
6. Гостиная 12,24 м²	стены		**К1**	Farrow & Ball No. 2003	Farrow & Ball · Modern Emulsion	матовая	1	86	22,4 м²
	акцент А		**К7**	Farrow & Ball No. 43	Farrow & Ball · Modern Emulsion	матовая	1	11.8	9,9 м²
	потолок		**К3**	Tikkurila G503	Tikkurila · Euro Power 7	глубокомат.	2	89	12,2 м²
	пол		**КМ1**	по образцу	инженерная доска · аналог по хар.				12,2 м²
	плинтус		**К4**	Farrow & Ball No. 2003	МДФ · в цвет Farrow & Ball			86	13,3 м
7. Спальня 13,9 м²	стены		**К1**	Farrow & Ball No. 2003	Farrow & Ball · Modern Emulsion	матовая	1	86	23,4 м²
	акцент В		**К8**	Farrow & Ball No. 34	Farrow & Ball · Modern Emulsion	матовая	1	22	12,9 м²
	потолок		**К3**	Tikkurila G503	Tikkurila · Euro Power 7	глубокомат.	2	89	13,9 м²
	пол		**КМ1**	по образцу	инженерная доска · аналог по хар.				13,9 м²
	плинтус		**К4**	Farrow & Ball No. 2003	МДФ · в цвет Farrow & Ball			86	14,8 м

Перечень выкрасов на согласование

№	Код	Бренд / веер	Пом. / стена	Подложка	Формат	Статус
1	No. 2003	Farrow & Ball	1, 4, 5, 6, 7	ГКЛ с грунтом; МДФ под эмаль	600×1000; 300×600	к выполнению
2	No. 30	Farrow & Ball	1 В	ГКЛ с грунтом	600×1000	к выполнению
3	G503	Tikkurila	1, 2, 3, 4, 5, 6, 7	ГКЛ с грунтом	600×1000	к выполнению
4	No. 281	Farrow & Ball	5 В	ГКЛ с грунтом	600×1000	к выполнению
5	No. 43	Farrow & Ball	6 А	ГКЛ с грунтом	600×1000	к выполнению
6	No. 34	Farrow & Ball	7 В	ГКЛ с грунтом	600×1000	к выполнению

Примечания

1. Цвет на листе и на экране — ориентир. До покраски — выкрас на объекте: не меньше А3 (или лист ГКЛ), на грунте под эту краску, не на белой шпаклёвке, в 2 слоя; на обороте — код, бренд, веер, дата. Смотреть днём и вечером, рядом с образцами пола и плитки; к основному цвету стен — ещё 2 соседних оттенка. Красить только в цвет утверждённого выкраса.
2. Краску заказывать по коду из графы «Система и код цвета» у бренда этого кода, не «аналогом» другого; весь объём одного кода — одной партией, колеруемую краску — за один проход машины.
3. Площади — те же, что в ведомости отделки (лист С1); сколько краски заказать — в спецификации отделочных материалов (лист С3).

Схема квартиры: цвет стен и акценты (б/м)

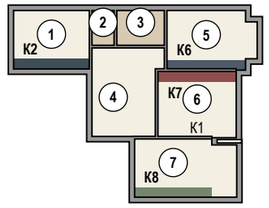


Схема палитры проекта

Стиль: Современный (контемпорари) 60% + Тихая роскошь (quiet luxury) 40% · схема: комплементарная

основной	основной	основной	второстепенный	второстепенный	второстепенный	акцентный	акцентный	акцентный	акцентный	акцентный	акцентный	акцентный	акцентный
Tikkurila G503	Farrow & Ball No. 2003	Tikkurila V503	Farrow & Ball No. 239	NCS S 2010-Y30R	Tikkurila H497	NCS S 7010-Y50R	NCS S 6020-G70Y	Farrow & Ball No. 238	Farrow & Ball No. 43	Farrow & Ball No. 30	Farrow & Ball No. 281	Farrow & Ball No. 43	Farrow & Ball No. 34
Calla LRV 89 потолок 1,2,3,4,5,6,7; текстиль/декор 1,5,6,7	Pointing LRV 86 стены 1,4,5,6,7; плинтус 1,4,5,6,7	Winter LRV 86 в отделке не применён	Shaded White LRV 63 текстиль/декор 1,5,6,7	светлый кэмел LRV 60 текстиль/декор 2	Pumice LRV 57 в отделке не применён	кофе / табак LRV 8 текстиль/декор 6	олива LRV 12 в отделке не применён	Bancha LRV 14 в отделке не применён	Mouse's Back LRV 26 в отделке не применён	Hague Blue — глубокий сине-зелёный LRV 7 акцент 1; текстиль/декор 1	Stiffkey Blue — чернильный синий LRV 10.1 акцент 5; текстиль/декор 7	Eating Room Red — брусничный красный LRV 11.8 акцент 6; текстиль/декор 6	Calke Green — традиционный шалфей LRV 22 акцент 7; текстиль/декор 3,6,7

План 60/30/10

60%	30%	10%

Окраска, факт — по площади стен, акцентов, потолков

81%	19%

окрашено всего 222,8 м²; второстепенный тон несут мебель и текстиль


Условные обозначения

- **К1** Farrow & Ball No. 2003 · Pointing · Modern Emulsion · матовая · кл. 1
- **К2** Farrow & Ball No. 30 · Hague Blue — глубокий сине-зелёный · Euro Power 7, колеровка по NCS · матовая · кл. 1
- **К3** Tikkurila G503 · Calla · Euro Power 7 · глубокомат. · кл. 2
- **К4** Farrow & Ball No. 2003 · Pointing · МДФ
- **К5** Tikkurila G503 · Calla · Euro Power 7 · матовая · кл. 1
- **К6** Farrow & Ball No. 281 · Stiffkey Blue — чернильный синий · Euro Power 7, колеровка по NCS · матовая · кл. 1
- **К7** Farrow & Ball No. 43 · Eating Room Red — брусничный красный · Modern Emulsion · матовая · кл. 1
- **К8** Farrow & Ball No. 34 · Calke Green — традиционный шалфей · Modern Emulsion · матовая · кл. 1
- дерево (доска, паркет, ламинат) — рисунок досок
- керамогранит, плитка, камень — сетка швов по формату
- **КМ1** аналог: инженерная доска, дуб натуральный, масло, 1-полосная, 14/4 мм
- **КМ2** плитка · аналог: керамогранит под травертин, матовый, 600×1200×9 мм
- **КМ3** аналог: керамогранит ректифицированный под травертин, матовый, 600×600×9 мм
- **КМ4** аналог: керамогранит ректифицированный под травертин, матовый, 600×1200×9 мм
- **КМ5** аналог: керамогранит под травертин, матовый, 1200×600×9 мм

К — краска, КМ — отделочный материал (тон КМ — по описанию, эталон — образец материала); кл. — класс истирания (1 — самый стойкий к мытью); LRV — светлота цвета: 0 — чёрный, 100 — белый

	Лист	№ док.	Подпись	Дата	Проект: Квартира 68 м², элитный модерн			
Дизайнер	Кырлан А.С.			13.11.26	Колерная карта	Стадия	Лист	Листов
Проверил						П	19	94
Н. контр.								
Утв.								

выпуск 13.11.2026 № c38d47cb31 · стр. 19 из 94

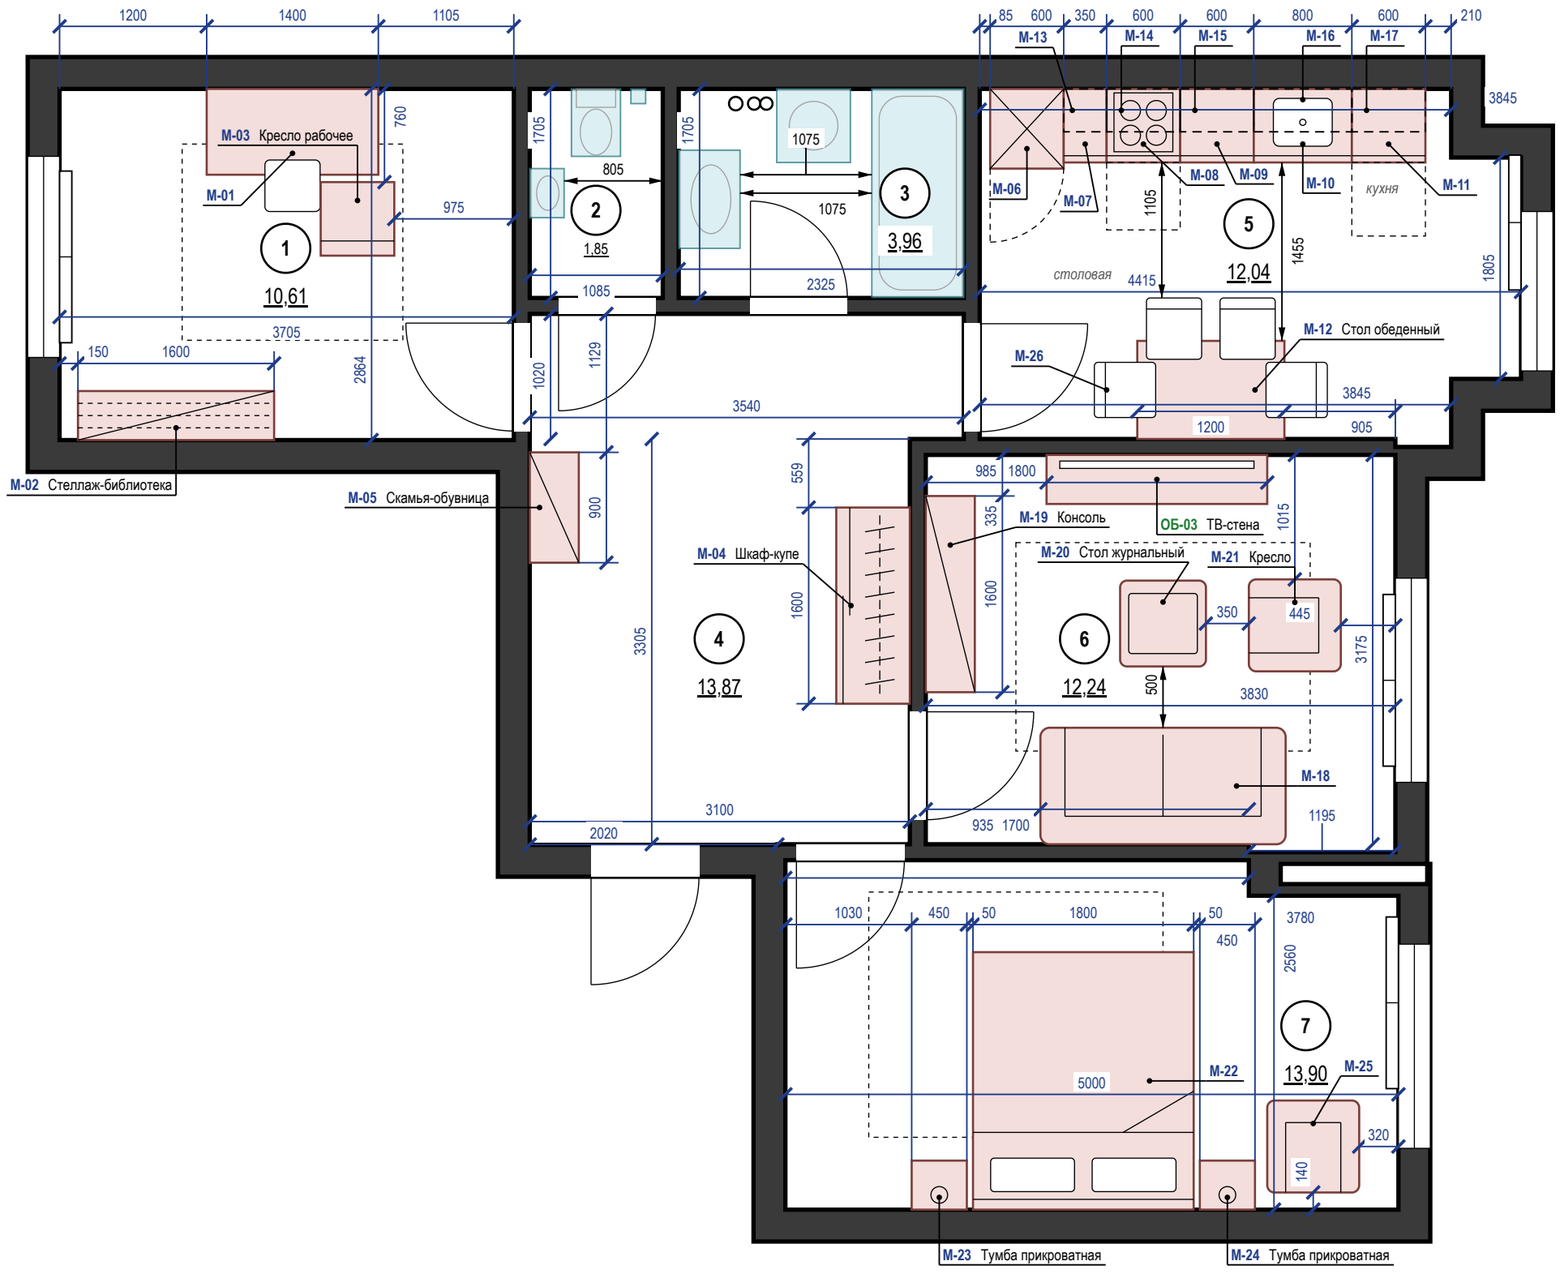

Экспликация помещений

лист 14 · на плане — номера в марках

Ведомость мебели и оборудования

Марка	Наименование	Ш×Г×В, мм	Пом.	Кол.
M-01	Стол письменный 1400×700	1400×700×750	1	1
M-02	Стеллаж-библиотека встроенный 1600×400	1600×400×2200	1	1
M-03	Кресло рабочее	600×600×900	1	1
M-04	Шкаф-купе 1600×600 до потолка	1600×600×2450	4	1
M-05	Скамья-обувница 900×400	900×400×450	4	1
M-06	Колонна с холодильником встроенным;	600×650×2200	5	1
M-07	Модуль узкий	350×600×900	5	1
M-08	Модуль с варочной панелью	600×600×900	5	1
M-09	Модуль с ящиками	600×600×900	5	1
M-10	Модуль под мойку; столешница	800×600×900	5	1
M-11	Посудомоечная машина встроенная 600	600×600×900	5	1
M-12	Стол обеденный 1200×800	1200×800×750	5	1
M-13	Навесной шкаф	350×350×900	5	1
M-14	Вытяжка встроенная в навесной шкаф	600×350×800	5	1
M-15	Навесной шкаф	600×350×900	5	1
M-16	Навесной шкаф с сушкой	800×350×900	5	1
M-17	Навесной шкаф	600×350×900	5	1
ОБ-03	ТВ-стена	1800×400×450	6	1
M-18	Диван 2000×950 с низкой спинкой	2000×950×850	6	1
M-19	Консоль 1600×400	1600×400×750	6	1
M-20	Стол журнальный круглый Ø700	700×700×400	6	1
M-21	Кресло 750×750	750×750×800	6	1
M-22	Кровать 1800×2100	1800×2100×900	7	1
M-23	Тумба прикроватная левая	450×400×500	7	1
M-24	Тумба прикроватная правая	450×400×500	7	1
M-25	Кресло 750×750 в эркере	750×750×800	7	1
M-26	Стул обеденный к столу M-12	450×500×820	5	4

Ш — вдоль стены (изголовья), Г — от стены (длина кровати)

Материалы, модели, допуск замены — лист 21

Примечания

1. Размеры — в мм от чистовых поверхностей стен; габариты предметов (Ш×Г×В) — в ведомости мебели, лист 21, на плане марка и короткое имя; размеры мебели уточнить после отделочных работ; общие указания — лист 12.
2. У позиций M-01, M-06, M-07, M-08, M-09, M-10, M-11, M-13, M-14, M-15, M-16, M-17, M-18, M-22, M-25, M-26 на плане только марка: наименование и габарит — в спецификации, лист 21.
3. Стулья обеденной группы (M-26 — 4 шт.) показаны в рабочем положении, задвинутыми под столешницу на 150 мм.

	Лист	№ док.	Подпись	Дата	Проект: Квартира 68 м², элитный модерн	М 1:50		
Дизайнер	Кырлан А.С.			13.11.26	План размещения мебели и оборудования	Стадия	Лист	Листов
Проверил						П	20	94
Н. контр.								
Утв.								

Поз.	Наименование и техническая характеристика	Тип, марка, обозначение документа, опросного листа	Код продукции	Поставщик	Ед. измерения	Кол.	Масса 1 ед., кг	Примечание
	Мебель встроенная и корпусная (изготовление по чертежам мебельщика)							
М-04	Шкаф-купе 1600×600 до потолка, двери — шпон ореха и бронзовое зеркало; корпус ЛДСП 16 мм; фасады — МДФ, шпон / эмаль 18 мм; вставка — зеркало серебро 4 мм на безопасной плёнке, в профиле двери; Ш×Г×В 1600×600×2450 мм	—	—	изготовление на заказ	шт.	1	—	пом. 4
М-06	Колонна с холодильником встроенным; фасады — МДФ: шпон американского ореха (нижние модули) и эмаль пыльно-синяя с узкой филёнкой (колонны), латунные ручки-скобы; фурнитура — латунь брашированная; корпус ЛДСП 16 мм; фрезеровка-рейка 30 мм, скрытые петли; Ш×Г×В 600×650×2200 мм	—	—	изготовление на заказ	шт.	1	—	пом. 5; крепление к стене
М-07	Модуль узкий с выдвижными ящиками 350; корпус ЛДСП 16 мм; фасады — МДФ, шпон американского ореха, фрезеровка-рейка 30 мм, скрытые петли; Ш×Г×В 350×600×900 мм	—	—	изготовление на заказ	шт.	1	—	пом. 5
М-08	Модуль с варочной панелью и духовым шкафом; корпус ЛДСП 16 мм; фасады — МДФ, шпон американского ореха, фрезеровка-рейка 30 мм, скрытые петли; Ш×Г×В 600×600×900 мм	—	—	изготовление на заказ	шт.	1	—	пом. 5
М-09	Модуль с ящиками; под встраиваемую технику: кофемашина; корпус ЛДСП 16 мм; фасады — МДФ, шпон американского ореха, фрезеровка-рейка 30 мм, скрытые петли; Ш×Г×В 600×600×900 мм	—	—	изготовление на заказ	шт.	1	—	пом. 5
М-10	Модуль под мойку; столешница — мрамор с яркой прожилкой (типа Calacatta Viola), 20 мм, фартук одним слэбом; корпус ЛДСП 16 мм; фасады — МДФ, шпон американского ореха, фрезеровка-рейка 30 мм, скрытые петли; Ш×Г×В 800×600×900 мм	—	—	изготовление на заказ	шт.	1	—	пом. 5
М-11	Модуль под встраиваемую ПММ 60; без корпуса (ниша между соседними модулями); фасад на дверь машины — МДФ, шпон американского ореха, фрезеровка-рейка 30 мм, скрытые петли; цоколь; Ш×Г×В 600×600×900 мм	—	—	изготовление на заказ	шт.	1	—	пом. 5
М-13	Навесной шкаф; корпус ЛДСП 16 мм; фасады — МДФ, эмаль глубокоматовая в цвет стен, без ручек 18 мм; Ш×Г×В 350×350×900 мм	—	—	изготовление на заказ	шт.	1	—	пом. 5
М-14	Вытяжка встроенная в навесной шкаф, рециркуляция до обмера вентканала; корпус ЛДСП 16 мм; фасады — МДФ, эмаль глубокоматовая в цвет стен, без ручек 18 мм; Ш×Г×В 600×350×800 мм	—	—	изготовление на заказ	шт.	1	—	пом. 5
М-15	Навесной шкаф; корпус ЛДСП 16 мм; фасады — МДФ, эмаль глубокоматовая в цвет стен, без ручек 18 мм; Ш×Г×В 600×350×900 мм	—	—	изготовление на заказ	шт.	1	—	пом. 5
М-16	Навесной шкаф с сушкой; корпус ЛДСП 16 мм; фасады — МДФ, эмаль глубокоматовая в цвет стен, без ручек 18 мм; Ш×Г×В 800×350×900 мм	—	—	изготовление на заказ	шт.	1	—	пом. 5
М-17	Навесной шкаф; корпус ЛДСП 16 мм; фасады — МДФ, эмаль глубокоматовая в цвет стен, без ручек 18 мм; Ш×Г×В 600×350×900 мм	—	—	изготовление на заказ	шт.	1	—	пом. 5
	Мебель покупная							
М-01	Стол письменный 1400×700, шпон ореха, кожаная вставка, латунные опоры; дерево — орех американский, металл латунь; Ш×Г×В 1400×700×750 мм	аналог: Ш×Г×В 1400×700×750 мм, дерево — орех американский	—	аналог по характеристикам	шт.	1	—	пом. 1; замена ≤ габарита
М-02	Стеллаж-библиотека встроенный 1600×400 до 2200, шпон американского ореха, полкодержатели — латунь; корпус и полки — МДФ 19 мм, масло; полкодержатели и кант — латунь брашированная, дерево — орех американский, металл латунь; Ш×Г×В 1600×400×2200 мм	аналог: Ш×Г×В 1600×400×2200 мм, корпус и полки МДФ 19 мм	—	аналог по характеристикам	шт.	1	—	пом. 1; крепление к стене; замена ≤ габарита
М-03	Кресло рабочее, кожа коньячная, основание — латунь брашированная; обивка кожа натуральная, металл — латунь; Ш×Г×В 600×600×900 мм	аналог: Ш×Г×В 600×600×900 мм, обивка кожа натуральная	—	аналог по характеристикам	шт.	1	—	пом. 1; замена ≤ габарита
М-05	Скамья-обувница 900×400, дуб натуральный, с сушилкой для обуви (предложение); дерево — дуб натуральный; Ш×Г×В 900×400×450 мм	аналог: Ш×Г×В 900×400×450 мм, дерево — дуб натуральный	—	аналог по характеристикам	шт.	1	—	пом. 4; замена ≤ габарита
М-12	Стол обеденный 1200×800, мраморная столешница, опора латунь; стулья с мягкой спинкой, 4 шт.; дерево — дуб натуральный; Ш×Г×В 1200×800×750 мм	аналог: Ш×Г×В 1200×800×750 мм, дерево — дуб натуральный	—	аналог по характеристикам	шт.	1	—	пом. 5; замена ≤ габарита
М-26	Стул обеденный к столу М-12; обивка — ткань, цвет Farrow & Ball No. 201; каркас — дуб натуральный; Ш×Г×В 450×500×820 мм	аналог: Ш×Г×В 450×500×820 мм, обивка — ткань	—	аналог по характеристикам	шт.	4	—	пом. 5; замена ≤ габарита
М-18	Диван 2000×950 с низкой спинкой, шерстяное букле, латунный цоколь; обивка букле; Ш×Г×В 2000×950×850 мм	аналог: Ш×Г×В 2000×950×850 мм, обивка букле	—	аналог по характеристикам	шт.	1	—	пом. 6; замена ≤ габарита
М-19	Консоль 1600×400, шпон ореха, рифлёные фасады, мраморная столешница, латунные опоры; дерево — орех американский, металл — латунь; Ш×Г×В 1600×400×750 мм	аналог: Ш×Г×В 1600×400×750 мм, дерево — орех американский	—	аналог по характеристикам	шт.	1	—	пом. 6; крепление к стене; замена ≤ габарита

Примечания

1. Позиции мебели совпадают с марками на плане расстановки; размеры Ш×Г×В — Ш вдоль стены, Г от стены.
2. Размеры и привязки плана расстановки — в мм от чистовых поверхностей стен: слой штукатурки 20 мм по блоку и 5 мм шпаклёвки по ГКЛ учтён; привязки — от стен и углов помещения, а не от другой мебели.
3. План расстановки не является документацией для изготовления мебели. Встроенная и корпусная мебель изготавливается по чертежам мебельщика после контрольного обмера (после штукатурки); «стена в стену» — с зазором 10 мм с каждой стороны или с компенсаторами; графы «Тип, марка» и «Код продукции» для неё не заполняются (ГОСТ 21.110-2013).
4. Покупные изделия — аналог по характеристикам: заменять только на изделия не больше указанного габарита и того же материала и цвета.
5. Материал и цвет, не указанные в данных изделия, приняты по концепции: тон дерева — по полу, обивка — по вторичному цвету палитры; образцы согласовать до заказа.
6. Масса 1 ед. для изделий до 25 кг не указывается. Техника — по монтажным схемам изготовителя; выводы — по листам ЭОМ и ВК.

	Лист	№ док.	Подпись	Дата	Проект: Квартира 68 м², элитный модерн			
Дизайнер	Кырлан А.С.			13.11.26	Спецификация мебели и оборудования	Стадия	Лист	Листов
Проверил						П	21	94
Н. контр.								
Утв.								

Поз.	Наименование и техническая характеристика	Тип, марка, обозначение документа, опросного листа	Код продукции	Поставщик	Ед. измерения	Кол.	Масса 1 ед., кг	Примечание
М-20	Стол журнальный круглый Ø700, столешница — мрамор с бордовой прожилкой (типа Calacatta Viola) 20 мм, основание латунь брашированная; металл — латунь; Ш×Г×В 700×700×400 мм	аналог: Ш×Г×В 700×700×400 мм, металл — латунь	—	аналог по характеристикам	шт.	1	—	пом. 6; замена ≤ габарита
М-21	Кресло 750×750, бархат хлопковый бордо, опоры — латунь брашированная; обивка бархат, металл — латунь, цвет Farrow & Ball No. 43; Ш×Г×В 750×750×800 мм	аналог: Ш×Г×В 750×750×800 мм, обивка бархат	—	аналог по характеристикам	шт.	1	—	пом. 6; замена ≤ габарита
ОБ-03	ТВ-стена: панели шпон ореха с латунным профилем, тумба подвесная 1800×400 с мраморной столешницей, ТВ 55" дерево — орех американский, металл — латунь; Ш×Г×В 1800×400×450 мм	аналог: Ш×Г×В 1800×400×450 мм, дерево — орех американский	—	аналог по характеристикам	шт.	1	—	пом. 6; замена ≤ габарита
М-22	Кровать 1800×2100, мягкое изголовье до 1300 мм, бархат, латунный кант; обивка кожа натуральная, дерево — дуб натуральный; Ш×Г×В 1800×2100×900 мм	аналог: Ш×Г×В 1800×2100×900 мм, обивка кожа натуральная	—	аналог по характеристикам	шт.	1	—	пом. 7; замена ≤ габарита
М-23	Тумба прикроватная левая, дуб натуральный; дерево — дуб натуральный; Ш×Г×В 450×400×500 мм	аналог: Ш×Г×В 450×400×500 мм, дерево — дуб натуральный	—	аналог по характеристикам	шт.	1	—	пом. 7; замена ≤ габарита
М-24	Тумба прикроватная правая, дуб натуральный; дерево — дуб натуральный; Ш×Г×В 450×400×500 мм	аналог: Ш×Г×В 450×400×500 мм, дерево — дуб натуральный	—	аналог по характеристикам	шт.	1	—	пом. 7; замена ≤ габарита
М-25	Кресло 750×750 в эркере, шерстяное букле молочное, опоры — латунь брашированная; обивка букле, металл — латунь; Ш×Г×В 750×750×800 мм	аналог: Ш×Г×В 750×750×800 мм, обивка букле	—	аналог по характеристикам	шт.	1	—	пом. 7; замена ≤ габарита
	Техника встраиваемая и бытовая (покупные изделия), светильники под розетки							
	Стиральная машина, место по листу ВК (ОБ-01); Ш×Г 600×600 мм	аналог по характеристикам: фронтальная загрузка, в плане 600 × 600 мм (ширина × глубина), по листу ВК	—	по выбору заказчика до изготовления мебели	шт.	1	—	пом. 3; по схеме изготовителя
	Сушильная машина встраиваемая, у М-05	аналог по характеристикам: тип загрузки — по листу ВК, по листу ВК	—	по выбору заказчика до изготовления мебели	шт.	1	—	пом. 4; по схеме изготовителя
	Холодильник встраиваемый, в модуле М-06	аналог по характеристикам: полновстраиваемый под фасад, ниша 1780 × 560 × 550 мм, вентиляция решётка в цоколе, выход сверху	—	по выбору заказчика до изготовления мебели	шт.	1	—	пом. 5; по схеме изготовителя
	Духовой шкаф встраиваемый, в модуле М-08	аналог по характеристикам: 60 см, лицевая панель 595 мм, ниша 560 × 600, глубина ≥ 550 мм, вентиляция за прибором	—	по выбору заказчика до изготовления мебели	шт.	1	—	пом. 5; по схеме изготовителя
	Посудомоечная машина встраиваемая, в модуле М-11; ниша 600 мм	аналог по характеристикам: полновстраиваемая 60 см под фасад, ниша 600 × 862 мм, навеска фасада в комплекте	—	по выбору заказчика до изготовления мебели	шт.	1	—	пом. 5; по схеме изготовителя
	Вытяжка встраиваемая, в модуле М-14	аналог по характеристикам: производительность — по расчёту ОВ, шум ≤ 55 дБ(А)	—	по выбору заказчика до изготовления мебели	шт.	1	—	пом. 5; по схеме изготовителя
	Варочная панель встраиваемая, индукционная, в модуле М-08	аналог по характеристикам: индукционная 60 см, вырез 560 × 490 мм по шаблону модели	—	по выбору заказчика до изготовления мебели	шт.	1	—	пом. 5; по схеме изготовителя
	Кофемашина встраиваемая, в модуле М-09	аналог по характеристикам: встраиваемая автоматическая 45 см, ниша 560 × 455, глубина ≥ 550 мм, низ ниши 900 мм от пола (чашка под носик), вывод воды не требуется (бак)	—	по выбору заказчика до изготовления мебели	шт.	1	—	пом. 5; вывод Р8 (ЭОМ)
	Кондиционер настенный (сплит-система), внутренний блок, КВ-1, стена А, низ +2,200 — предложено	аналог по характеристикам: настенный инверторный, 2,5 кВт, блок 900×300×210 мм, дренаж наружу (помпа), трасса фреона — по паспорту модели	—	по выбору заказчика до изготовления мебели	шт.	1	—	пом. 6; предложено, решает заказчик; вывод ЭВ4 (ЭОМ)
	Кондиционер настенный (сплит-система), внутренний блок, КВ-2, стена Г, низ +2,200 — предложено	аналог по характеристикам: настенный инверторный, 2,5 кВт, блок 900×300×210 мм, дренаж наружу (помпа), трасса фреона — по паспорту модели	—	по выбору заказчика до изготовления мебели	шт.	1	—	пом. 7; предложено, решает заказчик; вывод ЭВ5 (ЭОМ)
	Торшер, у поз. М-18; абажур — ткань или опаловое стекло; лампа 3000 К	—	—	аналог по характеристикам	шт.	1	—	пом. 6; розетка Р13 (ЭОМ)

	Лист	№ док.	Подпись	Дата
Дизайнер	Кырлан А.С.			13.11.26
Проверил				
Н. контр.				
Утв.				

Проект: Квартира 68 м², элитный модерн

Спецификация мебели и оборудования (продолжение)

Стадия	Лист	Листов
П	22	94

Поз.	Наименование и техническая характеристика	Тип, марка, обозначение документа, опросного листа	Код продукции	Поставщик	Ед. измерения	Кол.	Масса 1 ед., кг	Примечание
	Торшер, у поз. М-18; абажур — ткань или опаловое стекло; лампа 3000 K	—	—	аналог по характеристикам	шт.	1	—	пом. 6; розетка Р36 (ЭОМ)
	Торшер, у поз. М-18; абажур — ткань или опаловое стекло; лампа 3000 K	—	—	аналог по характеристикам	шт.	1	—	пом. 6; розетка Р37 (ЭОМ)
	Текстиль							
Т1	Портьеры в пол на потолочном карнизе, бархат хлопковый, светлый серо-бежевый; хлопок 100 %, подкладка полиэстер; цвет Farrow & Ball No. 201; карниз 2040 мм, высота 2575 мм, сборка 2	—	—	аналог по характеристикам	шт.	2	—	пом. 1
Т2	Тюль лён натуральный в пол; лён / хлопок / полиэстер по ткани; цвет Tikkurila G503; карниз 2040 мм, высота 2575 мм, сборка 2,5	—	—	аналог по характеристикам	шт.	1	—	пом. 1
Т16	Ковёр шерстяной ручной работы 1800×1600, глубокий сине-зелёный; шерсть 100 %; цвет Farrow & Ball No. 30; 1800×1600 мм	—	—	аналог по характеристикам	шт.	1	—	пом. 1; с подложкой
Т17	Полотенца для рук вафельные, шалфей, стопкой на столешнице тумбы умывальника; хлопок 100 %; цвет Farrow & Ball No. 34	—	—	аналог по характеристикам	шт.	2	—	пом. 3
Т3	Рулонная штора в проёме окна, ткань блэкаут; полиэстер 100 %; цвет Farrow & Ball No. 201; карниз 1260 мм, высота 1460 мм	—	—	аналог по характеристикам	шт.	1	—	пом. 5
Т4	Портьеры в пол на потолочном карнизе, бархат хлопковый, шалфей; хлопок 100 %, подкладка полиэстер; цвет Farrow & Ball No. 34; карниз 2065 мм, высота 2575 мм, сборка 2	—	—	аналог по характеристикам	шт.	2	—	пом. 6
Т5	Тюль лён натуральный в пол; лён / хлопок / полиэстер по ткани; цвет Tikkurila G503; карниз 2065 мм, высота 2575 мм, сборка 2,5	—	—	аналог по характеристикам	шт.	1	—	пом. 6
Т6	Ковёр фактурный шерсть с джутом 2400×1700, светлый серо-бежевый; шерсть / джут / хлопок по ткани; цвет Farrow & Ball No. 201; 2400×1700 мм	—	—	аналог по характеристикам	шт.	1	—	пом. 6; с подложкой
Т7	Подушки на диван, бархат хлопковый, бордо; хлопок 100 %; цвет Farrow & Ball No. 43	—	—	аналог по характеристикам	шт.	2	—	пом. 6
Т8	Подушки на диван, жаккард, шалфей; хлопок / вискоза; цвет Farrow & Ball No. 34	—	—	аналог по характеристикам	шт.	2	—	пом. 6
Т9	Плед шерсть мериноса с бахромой, молочный; шерсть / хлопок по ткани; цвет Tikkurila G503	—	—	аналог по характеристикам	шт.	1	—	пом. 6
Т10	Портьеры в пол в нише карниза, бархат хлопковый с блэкаут-подкладкой, чернильный синий; хлопок 100 %, подкладка полиэстер блэкаут; цвет Farrow & Ball No. 281; карниз 2265 мм, высота 2635 мм, сборка 2	—	—	аналог по характеристикам	шт.	2	—	пом. 7
Т11	Тюль лён натуральный в пол; лён / хлопок / полиэстер по ткани; цвет Tikkurila G503; карниз 2265 мм, высота 2635 мм, сборка 2,5	—	—	аналог по характеристикам	шт.	1	—	пом. 7
Т12	Ковёр фактурный шерсть с джутом 2400×2000, светлый серо-бежевый; шерсть / джут / хлопок по ткани; цвет Farrow & Ball No. 201; 2400×2000 мм	—	—	аналог по характеристикам	шт.	1	—	пом. 7; с подложкой
Т13	Подушки декоративные на кровать, бархат хлопковый, шалфей; хлопок 100 %; цвет Farrow & Ball No. 34	—	—	аналог по характеристикам	шт.	2	—	пом. 7
Т14	Подушки декоративные на кровать, жаккард, чернильный синий; хлопок / вискоза; цвет Farrow & Ball No. 281	—	—	аналог по характеристикам	шт.	2	—	пом. 7
Т15	Плед шерсть мериноса с бахромой в изножье кровати, светлый серо-бежевый; шерсть / хлопок по ткани; цвет Farrow & Ball No. 201	—	—	аналог по характеристикам	шт.	1	—	пом. 7
	Декор							
ДК15	Картина над столом М-01: холмы в утреннем тумане, масло, тонкая латунная рама 800×600; рама — латунь; 800×600 мм; низ на 1000 мм от пола	—	—	аналог по характеристикам	шт.	1	3	пом. 1; крепление: дюбель с крюком, 2 точки
ДК16	Картина на стене В: абстракция — охра, бордо и сусальное золото по молочному фону, тонкая латунная рама 700×900; рама — латунь; 700×900 мм; низ на 1050 мм от пола	—	—	аналог по характеристикам	шт.	1	3	пом. 1; крепление: дюбель с крюком, 2 точки
ДК17	Лампа настольная на столе М-01: основание и стойка — латунь брашированная, плафон-купол — матовое опаловое стекло; рама — латунь; 220×480 мм; на М-01	—	—	аналог по характеристикам	шт.	1	—	пом. 1
ДК9	Зеркало над умывальником, влагостойкое, с подсветкой; 400×800 мм; низ на 1200 мм от пола	—	—	аналог по характеристикам	шт.	1	5	пом. 2; крепление к стене
ДК22	Ваза-бутыль глазурованная, светлый кэмел, с сухоцветом (лагурус) — на полке короба инсталляции; 130×450 мм	—	—	аналог по характеристикам	шт.	1	—	пом. 2
ДК23	Свеча в янтарном стекле и аромадиффузор с ротанговыми палочками на латунном подносе — на полке короба; 220×200 мм	—	—	аналог по характеристикам	шт.	1	—	пом. 2

Поз.	Наименование и техническая характеристика	Тип, марка, обозначение документа, опросного листа	Код продукции	Поставщик	Ед. измерения	Кол.	Масса 1 ед., кг	Примечание
ДК24	Графика в тонкой латунной раме 300×400: ветка оливы, тушь; рама — латунь; 300×400 мм; низ на 1300 мм от пола	—	—	аналог по характеристикам	шт.	1	1	пом. 2; крепление: дюбель с крюком, 1 точка
ДК10	Зеркало над умывальником, влагостойкое, с подсветкой; 600×800 мм; низ на 1200 мм от пола	—	—	аналог по характеристикам	шт.	1	5	пом. 3; крепление к стене
ДК25	Керамический диспенсер для мыла и стакан, глазурь шалфей, на тумбе умывальника; 130×190 мм	—	—	аналог по характеристикам	шт.	1	—	пом. 3
ДК26	Свеча в янтарном стекле на латунном подносе, на бортике ванны у стены А; 200×160 мм; на С-04	—	—	аналог по характеристикам	шт.	1	—	пом. 3
ДК1	Зеркало над скамьёй 600×1200, тонкая латунная рама; рама — латунь; 600×1200 мм; низ на 700 мм от пола	—	—	аналог по характеристикам	шт.	1	6	пом. 4; крепление: дюбель 2 шт.
ДК2	Ваза с живыми цветами на обеденном столе; 200×300 мм; на М-12	—	—	аналог по характеристикам	шт.	1	—	пом. 5
ДК3	Часы настенные Ø300; 300×300 мм; низ на 1700 мм от пола	—	—	аналог по характеристикам	шт.	1	1	пом. 5; крепление к стене
ДК21	Ваза и чаша для фруктов ручной работы, глазурь молочная, на столешнице у окна; 320×300 мм; на М-11	—	—	аналог по характеристикам	шт.	1	—	пом. 5
ДК4	Картина над консолью М-19: крупная абстракция широкими мазками — бордо, охра, шалфей; холст, масло, тонкая латунная рама; рама — латунь; 1050×750 мм; низ на 1000 мм от пола	—	—	аналог по характеристикам	шт.	1	4	пом. 6; крепление к стене
ДК5	Картина над диваном М-18: горный пейзаж в утреннем тумане, холст, масло, тонкая латунная рама; рама — латунь; 1200×850 мм; низ на 1050 мм от пола	—	—	аналог по характеристикам	шт.	1	4	пом. 6; крепление к стене
ДК6	Оливковое дерево в кашпо Ø450; 450×450 мм	—	—	аналог по характеристикам	шт.	1	—	пом. 6
ДС1	Стеновые панели ТВ-стены: шпон американского ореха, швы — латунный Т-профиль; низ на 0 мм от пола	—	—	аналог по характеристикам	шт.	1	—	пом. 6
ДК11	Книги по искусству стопкой и свеча в латунном подсвечнике на журнальном столе; 280×150 мм; на М-20	—	—	аналог по характеристикам	шт.	1	—	пом. 6
ДК12	Чаша и низкая ваза ручной работы, глазурь шалфей, на журнальном столе; 250×180 мм; на М-20	—	—	аналог по характеристикам	шт.	1	—	пом. 6
ДК13	Лампа настольная на консоли М-19: основание — алебастр, арматура — латунь брашированная, абажур — лён молочный; рама — латунь; 220×480 мм; на М-19	—	—	аналог по характеристикам	шт.	1	—	пом. 6
ДК14	Вазы ручной работы разной высоты (360 и 240 мм), 2 шт., глазурь цвета табака, на торце консоли; 250×360 мм; на М-19	—	—	аналог по характеристикам	шт.	2	—	пом. 6
ДК7	Картина над изголовьем кровати М-22: пересекающиеся дуги, графика тушью и сусальным золотом, паспарту, тонкая латунная рама; рама — латунь; 900×650 мм; низ на 1100 мм от пола	—	—	аналог по характеристикам	шт.	1	4	пом. 7; крепление к стене
ДК8	Монстера в кашпо Ø450; 450×450 мм	—	—	аналог по характеристикам	шт.	1	—	пом. 7
ДК18	Зеркало в рост 600×1700 с арочным верхом, рама — латунь брашированная; рама — латунь; 600×1700 мм; низ на 200 мм от пола	—	—	аналог по характеристикам	шт.	1	12	пом. 7; крепление: анкер для пустотелых оснований, 4 шт.
ДК19	Книги стопкой и свеча в латунном подсвечнике на тумбе М-23; 280×140 мм; на М-23	—	—	аналог по характеристикам	шт.	1	—	пом. 7
ДК20	Ваза ручной работы с одной веткой, глазурь шалфей, на тумбе М-24; 180×260 мм; на М-24	—	—	аналог по характеристикам	шт.	1	—	пом. 7

	Лист	№ док.	Подпись	Дата
Дизайнер	Кырлан А.С.			13.11.26
Проверил				
Н. контр.				
Утв.				

Проект: Квартира 68 м², элитный модерн

Спецификация мебели и оборудования (продолжение)

Стадия	Лист	Листов
П	24	94

Ведомость изделий

Марка	Наименование	Пом.	Ш×Г×В, мм	Корпус	Фасад	Кромка, мм	Кол.
М-04	Шкаф-купе	4	1600×600×2450	ЛДСП 16	МДФ, шпон / эмаль 18 мм; вставка зеркало серебро 4 мм на безопасной плёнке, в профиле двери	0,4 / 1	1
М-06	Пенал: холодильник встр.	5	600×650×2200	ЛДСП 16	МДФ, шпон американского ореха, фрезеровка-рейка 30 мм, скрытые петли	0,4 / 1	1
М-07	Модуль нижний: ящики	5	350×600×900	ЛДСП 16	МДФ, шпон американского ореха, фрезеровка-рейка 30 мм, скрытые петли	0,4 / 1	1
М-13	Модуль навесной: полки	5	350×350×900	ЛДСП 16	МДФ, эмаль глубокоматовая в цвет стен, без ручек 18 мм	0,4 / 1	1
М-08	Модуль нижний: духовой шкаф, варочная	5	600×600×900	ЛДСП 16	МДФ, шпон американского ореха, фрезеровка-рейка 30 мм, скрытые петли	0,4 / 1	1
М-14	Модуль навесной: полки	5	600×350×800	ЛДСП 16	МДФ, эмаль глубокоматовая в цвет стен, без ручек 18 мм	0,4 / 1	1
М-09	Модуль нижний: ящики	5	600×600×900	ЛДСП 16	МДФ, шпон американского ореха, фрезеровка-рейка 30 мм, скрытые петли	0,4 / 1	1
М-15	Модуль навесной: полки	5	600×350×900	ЛДСП 16	МДФ, эмаль глубокоматовая в цвет стен, без ручек 18 мм	0,4 / 1	1
М-10	Модуль нижний: мойка	5	800×600×900	ЛДСП 16	МДФ, шпон американского ореха, фрезеровка-рейка 30 мм, скрытые петли	0,4 / 1	1
М-16	Модуль навесной: сушка	5	800×350×900	ЛДСП 16	МДФ, эмаль глубокоматовая в цвет стен, без ручек 18 мм	0,4 / 1	1
М-11	Модуль под ПММ 60: без корпуса, фасад на дверь машины	5	600×600×900	без корпуса	МДФ, шпон американского ореха, фрезеровка-рейка 30 мм, скрытые петли — на дверь машины (навеска из её комплекта), цоколь		1
М-17	Модуль навесной: полки	5	600×350×900	ЛДСП 16	МДФ, эмаль глубокоматовая в цвет стен, без ручек 18 мм	0,4 / 1	1

Ведомость встраиваемой техники

Поз.	Прибор	Ниша, вырез, мм	Вентиляция	Питание	Схема
М-06	Холодильник встраиваемый, ниша 1780	ниша 1780 × 560 × 550	решётка в цоколе, канал за корпусом, выход сверху	Р7: М-06, Н=2050 — над нишей холодильника, съёмная панель	по модели
М-08	Духовой шкаф встраиваемый, 60 см	ниша 560 × 600, глубина ≥ 550	зазор за шкафом, вырез в задней стенке	ЭВ2: М-08, Н=150 — под духовым шкафом, доступ через ящик	по модели
М-08	Варочная панель индукционная, 60 см	вырез в столешнице 560 × 490		ЭВ1: М-07, Н=600 — в соседнем модуле, за ящиком	по модели
М-10	Мойка врезная / подстольная с сифоном	вырез по шаблону, ориентир 700 × 480		смеситель — выводы ВК	по модели
М-11	Посудомоечная машина встраиваемая, 60 см	ниша 600 × 862 (от пола до низа столешницы)	зазор в цоколе, по схеме	Р6: М-11, Н=300 — за ПММ — перенести в соседний модуль	по модели
М-14	Вытяжка встраиваемая в навесной модуль, 60 см	низ ≥ 650 над панелью	воздуховод к вентканалу, короб до потолка	ЭВ3: М-14, Н=2200 — в навесном модуле	по модели

Ведомость фурнитуры


№	Фурнитура	Тип, размер	Изделия	Кол.
1	Система дверей купе: профиль, направляющие, ролики	на 2 двери	М-04	1
2	Ручка-профиль вертикальная	в цвет профиля	М-04	2
3	Полкодержатель с фиксацией	ø5 мм	М-04, М-06, М-13, М-14, М-15, М-17	40
4	Штанга овальная 30×15, L = 776	+ 2 держателя	М-04	1
5	Полка для обуви выдвижная наклонная	ширина 776	М-04	3
6	Опора регулируемая с цоколем на клипсах	ход 20 мм	М-04	6
7	Анкер по основанию стены	по таблице крепежа	М-04, М-13, М-14, М-15, М-16, М-17	15
8	Уголок крепления к стене от опрокидывания	стальной	М-04, М-06	4
9	Петля накладная 110° с доводчиком	чашка 35 мм	М-06, М-13, М-14, М-15, М-10, М-16, М-17	29
10	Ручка-профиль	латунь матовая	М-06, М-07, М-13, М-08, М-14, М-09, М-15, М-10, М-16, М-11, М-17	22
11	Опора кухонная регулируемая 100–120 мм	+ клипса цоколя	М-06, М-07, М-08, М-09, М-10	22
12	Направляющие полного выдвижения с доводчиком NL 500	пара	М-07, М-08, М-09	7
13	Навес регулируемый для навесного шкафа	пара на секцию	М-13, М-14, М-15, М-16, М-17	5
14	Шина монтажная	L = 290	М-13	1
15	Шина монтажная	L = 540	М-14, М-15, М-17	3
16	Сушка для посуды в шкаф	ширина 800	М-16	1
17	Шина монтажная	L = 740	М-16	1
18	Комплект навески фасада ПММ	из поставки машины	М-11	1

Примечания


1. Модели техники выбирает заказчик до изготовления мебели; ниши, вырезы и вентиляция — по монтажной схеме выбранной модели (условие гарантии), её номер вносится в ведомость.
2. Количество фурнитуры — по чертежам изделий; запас крепежа 5 %. Аналоги — по характеристикам (доводчик, нагрузка, ход).
3. Цвет корпусов, фасадов и профилей — по колерной карте проекта. Кромка — скрытые / видимые торцы, мм.

	Лист	№ док.	Подпись	Дата	Проект: Квартира 68 м², элитный модерн			
Дизайнер	Кырлан А.С.			13.11.26	Ведомости изделий, техники и фурнитуры	Стадия	Лист	Листов
Проверил						П	25	94
Н. контр.								
Утв.								


Фрагмент 1. Санузел, пом. 2 (М 1:40)

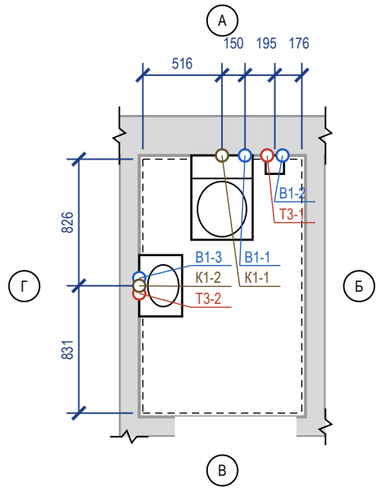

Фрагмент 2. Ванная, пом. 3 (М 1:40)

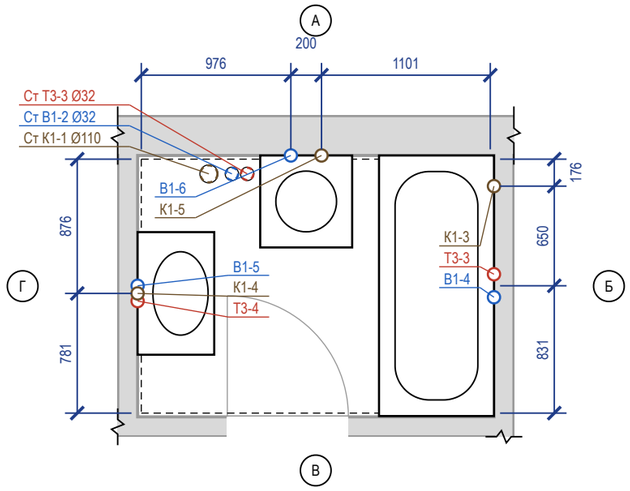

Фрагмент 3. Кухня-столовая, пом. 5 (М 1:40)

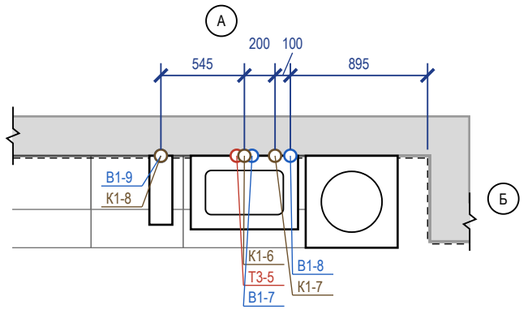

Ведомость привязок выводов

Код	Прибор	Ø	H, мм	Привязка от чист. стен, мм	Прим.
В1-1	С-01 унитаз подвесной	½"	1000	ст. А: 371 от Б	в раме инсталляции
К1-1	—"	Ø110	220	ст. А: 516 от Г	
В1-2	С-02 гигиенический душ	½"	750	ст. А: 126 от Б	межос. 100
Т3-1	—"	½"	750	ст. А: 226 от Б	межос. 100
В1-3	С-03 умывальник	½"	550	ст. Г: 776 от А	межос. 100
Т3-2	—"	½"	550	ст. Г: 781 от В	межос. 100
К1-2	—"	Ø40	500	ст. Г: 826 от А	
В1-4	С-04 ванна	½"	800	ст. Б: 756 от В	межос. 150
Т3-3	—"	½"	800	ст. Б: 751 от А	межос. 150
К1-3	—"	Ø50	50	ст. Б: 176 от А	
В1-5	С-05 умывальник	½"	550	ст. Г: 826 от А	межос. 100
Т3-4	—"	½"	550	ст. Г: 731 от В	межос. 100
К1-4	—"	Ø40	500	ст. Г: 781 от В	
В1-6	ОБ-01 стиральная машина	½"	600	ст. А: 976 от Г	кран машины
К1-5	—"	Ø40	600	ст. А: 1101 от Б	
В1-7	С-06 мойка кухонная	½"	600	ст. А: 1145 от Б	межос. 100
Т3-5	—"	½"	600	ст. А: 1245 от Б	межос. 100
К1-6	—"	Ø50	400	ст. А: 1195 от Б	
В1-8	ОБ-02 посудомоечная машина	½"	550	ст. А: 895 от Б	кран ПММ в шкафу мойки
К1-7	—"	Ø40	550	ст. А: 995 от Б	слив ПММ в шкафу мойки
В1-9	С-07 фильтр обратного осмоса	½"	550	ст. А: 1740 от Б	
К1-8	—"	Ø40	450	ст. А: 1740 от Б	

Условные обозначения


- вывод В1 (код — в ведомости привязок)
- вывод Т3 (код — в ведомости привязок)
- вывод К1 (код — в ведомости привязок)
- сантехприбор по расстановке (габарит модели)
- чистовая поверхность стены (от неё привязки)
- стояк «Ст К1-N / Ст В1-N» (ГОСТ 21.601), Ø мм
- стояк Т3 не на обмере — принят в шахте рядом со Ст В1, сверить
- линия обрыва (граница фрагмента)
- А — обозначение стены А–Г (как на развёртках)

Примечания


1. Привязки выводов даны от чистовых поверхностей стен (облицовка на сторону: санузел — 24 мм (штукатурка 10 + клей 5 + плитка 9); ванная — 24 мм (штукатурка 10 + клей 5 + плитка 9); кухня-столовая — 24 мм (фартук: штукатурка 10 + клей 5 + плитка 9)); эти же грани — на развёртках и в раскладке плитки. Высоты — от чистого пола помещения.
2. До черновой разводки сверить по паспорту выбранного прибора (смеситель, инсталляция, сифон).
3. Горячая вода (Т3) — слева от холодной (В1), если смотреть на прибор. Допуск установки выводов: ±5 мм в группе, ±20 мм у отдельно стоящих.
4. Расчёт систем водоснабжения и канализации и подбор оборудования выполняет проектная организация; лист задаёт места и высоты выводов.
5. Посудомоечная машина ОБ-02: кран и слив — отдельными выводами в шкафу мойки (не за машиной), до машины ≤ 1500 мм.
6. Ст К1-1, Ст В1-2, Ст Т3-3 на обмере не показаны: положение принято (исполнитель по плану заказчика), не замерено; положение сверить на объекте до разметки.
7. Стояки в коробах/шахтах не замоноличивать; стояк К1 в коробе — звукоизоляция стояка в коробе без жёсткого контакта с трубой; к арматуре и ревизиям — люк не меньше 300×400.

	Лист	№ док.	Подпись	Дата	Проект: Квартира 68 м², элитный модерн			М 1:40
Дизайнер	Кырлан А.С.			13.11.26	План выводов сантехники	Стадия	Лист	Листов
Проверил						П	26	94
Н. контр.								
Утв.								


План квартиры (М 1:200)

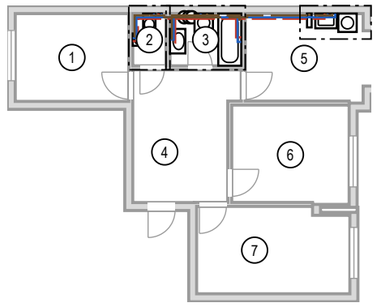


Фр. 3. Кухня-столовая (М 1:25)

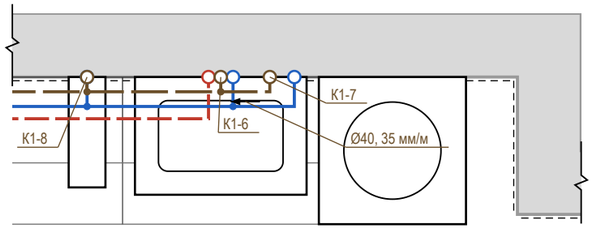

Фр. 1. Санузел (М 1:25)

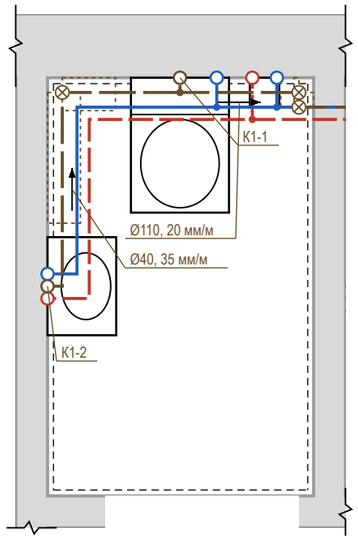

Фр. 2. Ванная (М 1:25)

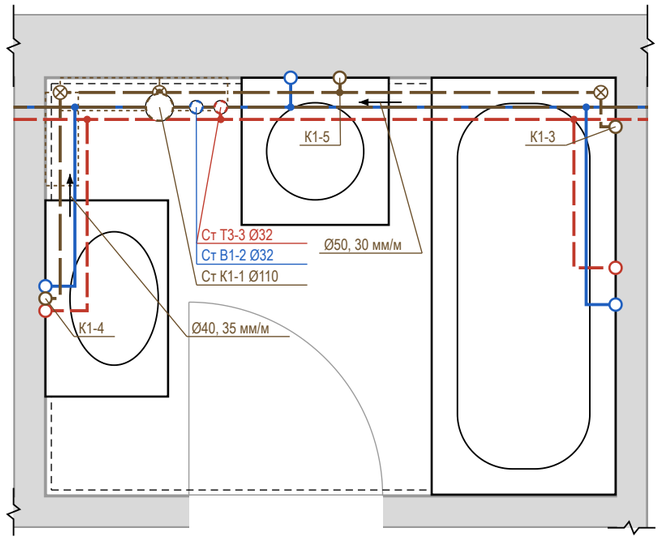

Условные обозначения


- В1 — водопровод хозяйственно-питьевой (ХВС), PP-R Ø20
- Т3 — горячее водоснабжение, подача (ГВС), PP-R Ø20
- К1 — канализация бытовая
- направление уклона К1 / пола: Ø, мм на 1 м
- ревизия (прочистка) К1 — доступ сохранить
- тройник (ответвление к прибору)
- короб К1 над чистым полом (ГКЛВ под плитку)
- вывод В1 (код — в ведомости привязок)
- вывод Т3 (код — в ведомости привязок)
- вывод К1 (код — в ведомости привязок)
- сантехприбор по расстановке (габарит модели)
- стояк «Ст К1-N / Ст В1-N» (ГОСТ 21.601), Ø мм
- стояк Т3 не на обмере — принят в шахте рядом со Ст В1, сверить
- линия обрыва (граница фрагмента)
- граница фрагмента на плане (Фр. N)

Профиль выпусков К1 (до врезки в стояк)

Выпуск	Прибор	Ø	L, м	i, мм/м	Δh, мм	Прокладка, мм
К1-1	С-01 унитаз подвесной	Ø110	1,26	20	25	в полу не помещается: 210 > 90; до решения
К1-6	С-06 мойка кухонная	Ø50	4,75	30	142	над полом за приборами
К1-3	С-04 ванна	Ø50	2,06	30	62	в полу не помещается: 187 > 90; до решения
К1-7	ОБ-02 посудомоечная машина	Ø40	4,95	35	173	над полом за приборами
К1-8	С-07 фильтр обратного осмоса	Ø40	4,20	35	147	над полом за приборами
К1-2	С-03 умывальник	Ø40	2,53	35	89	короб 160×110
К1-4	С-05 умывальник	Ø40	1,36	35	48	короб 120×110
К1-5	ОБ-01 стиральная машина	Ø40	0,85	35	30	короб 100×110

Короб h×b: h — от чистого пола, b — от чистовой стены. Стяжка 90 мм — лист полов.

Узел ввода В1, Т3 (по данным, без масштаба)

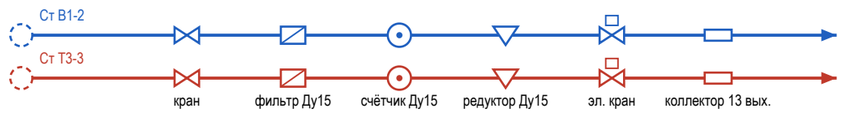

⊗ Ст К1-1: ревизия на стояке — люк в коробе


Примечания

1. Трассы принципиальные, построены от стояков вдоль стен помещений; фактическое положение фиксируется исполнительной схемой с привязками (фото с рулеткой) до закрытия.
2. Уклон К1 не менее 1/d и не более 150 мм/м (СП 30.13330.2020, п. 19.1), приняты практические уклоны; поворот — двумя отводами 45°, ревизия после поворота, доступ сохранить. Стояк К1 в коробе — звукоизоляция стояка в коробе, без жёсткого контакта короба с трубой.
3. Решение по К1: стяжка 90 мм не укрывает трубы (нужно Ø + Δh + 45 мм) — выпуски идут над чистым полом вдоль стен: К1-6, К1-7, К1-8 — за приборами и в раме инсталляции; К1-2, К1-4, К1-5 — в коробе ГКЛВ под плитку (размеры в профиле). Короба — на развёртках; отметку низа врезки в стояк замерить до черновых работ.
4. К1-1 (С-01 унитаз подвесной): Δh 25 + Ø110 + 45 = 210 мм > пирога 90 мм — в стяжке не помещается: подиум или подъём пола на 120 мм, короб 170×140 или прибор ближе к стояку — решение заказчика; до решения не выполнять.
5. К1-3 (С-04 ванна): Δh 62 + Ø50 + 45 = 187 мм > пирога 90 мм — в стяжке не помещается: подиум или подъём пола на 100 мм, короб 150×110 или прибор ближе к стояку — решение заказчика; до решения не выполнять.
6. Отводы К1-6 (4,7 м), К1-7 (4,9 м), К1-8 (4,2 м) длиннее 4 м без вентиляции — у прибора воздушный клапан Ø50 в доступном месте (за люком или в тумбе) либо вентилируемый отвод (EN 12056-2, табл. 4), подбор — проектная организация.
7. Узел ввода В1, Т3 — по данным проекта: кран → фильтр Ду15 → счётчик Ду15 → редуктор Ду15 → эл. кран → коллектор 13 вых.. Доступ к арматуре — через люк не меньше 300×400. Водопровод — в штробе стен или в коробах; трубы испытать давлением до закрытия (акт скрытых работ).
8. Расчёт систем, диаметры магистралей и подбор оборудования выполняет проектная организация; врезка и перенос стояков — по согласованию с управляющей организацией. Арматуру и привязки сверить по паспортам приборов.
9. Ведомость выводов (код, прибор, высота, привязка) — лист 26; на схеме — только коды.
10. Ст К1-1, Ст В1-2, Ст Т3-3 на обмере не показаны: положение принято (исполнитель по плану заказчика), не замерено; положение сверить на объекте до разводки.

	Лист	№ док.	Подпись	Дата	Проект: Квартира 68 м², элитный модерн			
Дизайнер	Кырлан А.С.			13.11.26	Схема разводки водопровода и канализации	Стадия	Лист	Листов
Проверил						П	27	94
Н. контр.								
Утв.								

выпуск 13.11.2026 № c38d47cb31 · стр. 27 из 94

Схема В1 (М 1:50)

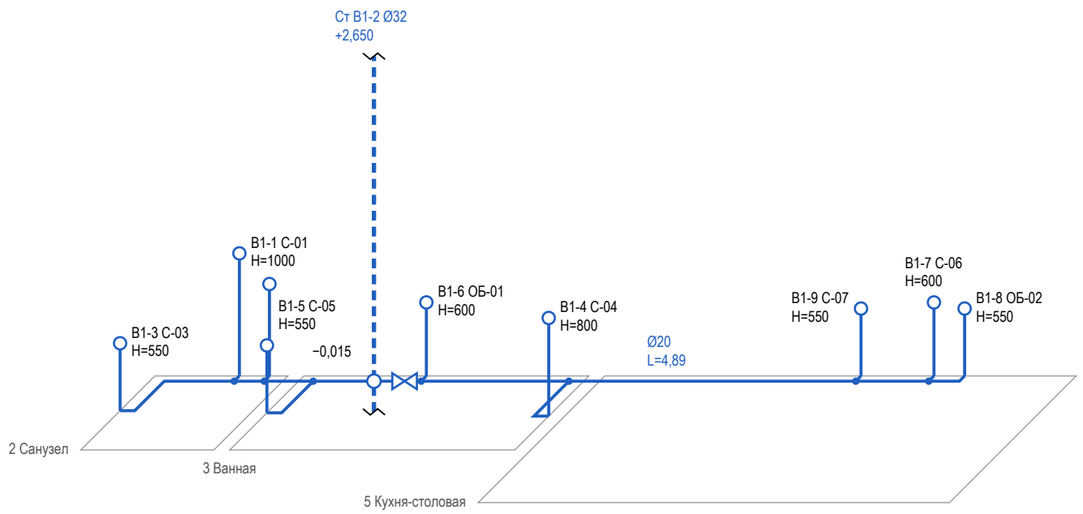

Ведомость выводов В1

Код	Прибор	H, мм	Ø, мм	Трасса, м
В1-8	ОБ-02 посудомоечная машина	550	20	4,89
В1-7	С-06 мойка кухонная	600	20	0,12
В1-9	С-07 фильтр обратного осмоса	550	20	0,12
В1-4	С-04 ванна	800	20	0,93
В1-3	С-03 умывальник	550	20	2,51
В1-5	С-05 умывальник	550	20	0,85
В1-1	С-01 унитаз подвесной	1000	20	0,12
В1-2	С-02 гигиенический душ	750	20	0,12
В1-6	ОБ-01 стиральная машина	600	20	0,12

Условные обозначения

- В1 — водопровод хозяйственно-питьевой (ХВС), PP-R Ø20
- вывод В1 (код — в ведомости привязок)
- стояк «Ст К1-N / Ст В1-N» (ГОСТ 21.601), Ø мм
- стояк в плане (на отметке пола); вертикаль — стояк по высоте, разрыв — перекрытие
- тройник (ответвление к прибору)
- кран шаровой
- стояк Т3 не на обмере — принят в шахте рядом со Ст В1, сверить

Примечания

1. Схема В1 построена по тем же трассам, что план разводки: положение в плане сохранено, глубина — в масштабе ×0,5. Трассы принципиальные; фактическое положение фиксируется исполнительной схемой до закрытия.
2. Высоты H — от чистого пола помещения, мм. Прокладка магистрали В1 по данным: коллекторная разводка, в стяжке пола, в стяжке пола, выше плиты перекрытия; отметка трасс — по пирогу пола.
3. Узел ввода В1 (кран, фильтр, счётчик, обратный клапан, кран) — на схеме разводки; состав узла ввода — по согласованию. Кран шаровой — на первом участке от стояка.
4. Ст В1-2 на обмере не показаны: положение принято (исполнитель по плану заказчика), не замерено; положение сверить на объекте до разводки.
5. Трубы испытать давлением до закрытия (акт скрытых работ, опрессовка по СП 73.13330.2016).
6. Диаметры, высоты выводов и места кранов — по паспортам выбранных приборов и расчёту проектной организации.
7. Расчёт систем, диаметры магистралей и подбор оборудования выполняет проектная организация.


	Лист	№ док.	Подпись	Дата
Дизайнер	Кырлан А.С.			13.11.26
Проверил				
Н. контр.				
Утв.				

Проект: Квартира 68 м², элитный модерн — **М 1:50**

Аксонометрическая схема В1 (холодное водоснабжение)	Стадия	Лист	Листов
	П	28	94

выпуск 13.11.2026 № c38d47cb31 · стр. 28 из 94

Схема Т3 (М 1:50)

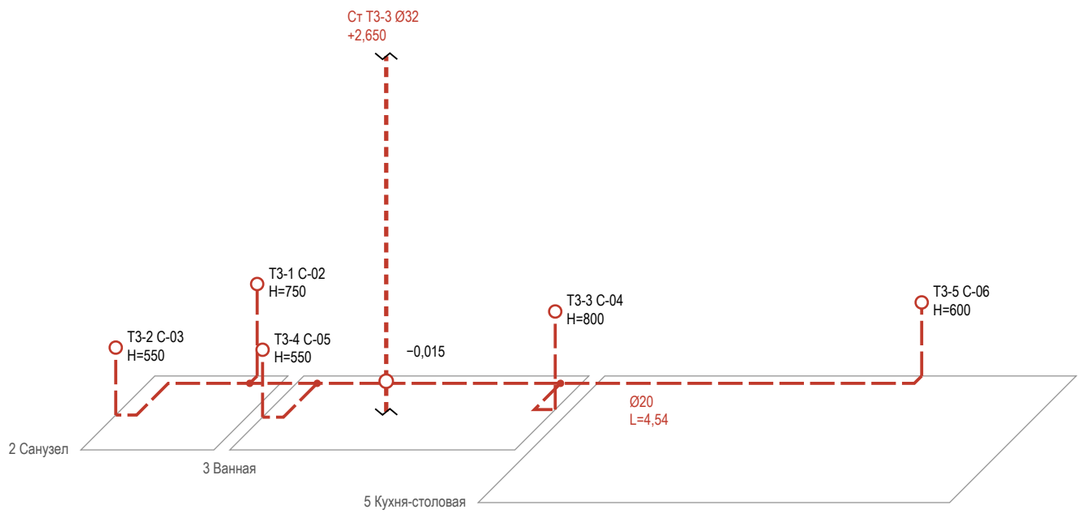

Ведомость выводов Т3

Код	Прибор	H, мм	Ø, мм	Трасса, м
Т3-5	С-06 мойка кухонная	600	20	4,54
Т3-2	С-03 умывальник	550	20	2,66
Т3-3	С-04 ванна	800	20	0,78
Т3-4	С-05 умывальник	550	20	0,95
Т3-1	С-02 гигиенический душ	750	20	0,17

Условные обозначения

- Т3 — горячее водоснабжение, подача (ГВС), PP-R Ø20
- вывод Т3 (код — в ведомости привязок)
- стояк «Ст К1-N / Ст В1-N» (ГОСТ 21.601), Ø мм
- стояк в плане (на отметке пола); вертикаль — стояк по высоте, разрыв — перекрытие
- тройник (ответвление к прибору)
- кран шаровой
- стояк Т3 не на обмере — принят в шахте рядом со Ст В1, сверить

Примечания

1. Схема Т3 построена по тем же трассам, что план разводки: положение в плане сохранено, глубина — в масштабе ×0,5. Трассы принципиальные; фактическое положение фиксируется исполнительной схемой до закрытия.
2. Высоты H — от чистого пола помещения, мм. Прокладка магистрали Т3 по данным: коллекторная разводка, в стяжке пола, в стяжке пола, выше плиты перекрытия; отметка трасс — по пирогу пола.
3. Узел ввода Т3 (кран, фильтр, счётчик, обратный клапан, кран) — на схеме разводки; состав узла ввода — по согласованию. Кран шаровой — на первом участке от стояка.
4. Циркуляция ГВС в данных не задана — циркуляционного трубопровода на схеме нет.
5. Ст Т3-3 на обмере не показаны: положение принято (исполнитель по плану заказчика), не замерено; положение сверить на объекте до разводки.
6. Трубы испытать давлением до закрытия (акт скрытых работ, опрессовка по СП 73.13330.2016).
7. Диаметры, высоты выводов и места кранов — по паспортам выбранных приборов и расчёту проектной организации.
8. Расчёт систем, диаметры магистралей и подбор оборудования выполняет проектная организация.


	Лист	№ док.	Подпись	Дата
Дизайнер	Кырлан А.С.			13.11.26
Проверил				
Н. контр.				
Утв.				

Проект: Квартира 68 м², элитный модерн — **М 1:50**

Аксонометрическая схема Т3 (горячее водоснабжение)	Стадия	Лист	Листов
	П	29	94

выпуск 13.11.2026 № c38d47cb31 · стр. 29 из 94

Схема К1 (М 1:50)

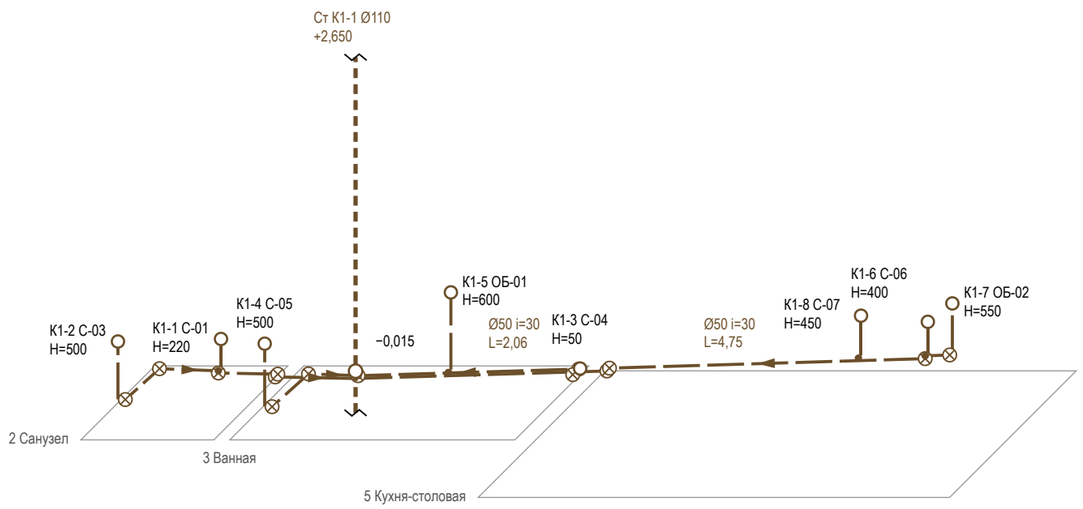

Ведомость выводов К1

Код	Прибор	H, мм	Ø, i	Трасса, м
К1-1	С-01 унитаз подвесной	220	110 i=20	1,26
К1-6	С-06 мойка кухонная	400	50 i=30	4,75
К1-3	С-04 ванна	50	50 i=30	2,06
К1-7	ОБ-02 посудомоечная машина	550	40 i=35	0,26
К1-8	С-07 фильтр обратного осмоса	450	40 i=35	0,06
К1-2	С-03 умывальник	500	40 i=35	1,33
К1-4	С-05 умывальник	500	40 i=35	1,30
К1-5	ОБ-01 стиральная машина	600	40 i=35	0,06

Условные обозначения

- К1 — канализация бытовая
- вывод К1 (код — в ведомости привязок)
- стояк «Ст К1-N / Ст В1-N» (ГОСТ 21.601), Ø мм
- стояк в плане (на отметке пола); вертикаль — стояк по высоте, разрыв — перекрытие
- направление уклона К1 / пола: Ø, мм на 1 м
- ⊗ ревизия (прочистка) К1 — доступ сохранить
- • тройник (ответвление к прибору)
- стояк Т3 не на обмере — принят в шахте рядом со Ст В1, сверить

Примечания

1. Схема К1 построена по тем же трассам, что план разводки: положение в плане сохранено, глубина — в масштабе ×0,5. Трассы принципиальные; фактическое положение фиксируется исполнительной схемой до закрытия.
2. Отметки — от плиты перекрытия: низ трубы у врезки в стояк — отметка из данных выпуска, к прибору труба поднимается на уклон i, мм/м (уклон не менее 1/d и не более 150 мм/м, СП 30.13330.2020, п. 19.1); чистый пол — выше плиты на стяжку (высота пирога пола). Высота выпуска прибора H — от чистого пола.
3. Ревизия — на повороте и в начале участка; стояк К1 в коробе с люком — звукоизоляция стояка в коробе; поворот — двумя отводами 45°.
4. Ст К1-1 на обмере не показаны: положение принято (исполнитель по плану заказчика), не замерено; положение сверить на объекте до разводки.
5. Трубы испытать давлением до закрытия (акт скрытых работ, опрессовка по СП 73.13330.2016).
6. Диаметры, высоты выводов и места кранов — по паспортам выбранных приборов и расчёту проектной организации.
7. Расчёт систем, диаметры магистралей и подбор оборудования выполняет проектная организация.


	Лист	№ док.	Подпись	Дата
Дизайнер	Кырлан А.С.			13.11.26
Проверил				
Н. контр.				
Утв.				

Проект: Квартира 68 м², элитный модерн — **М 1:50**


Аксонометрическая схема К1 (канализация)	Стадия	Лист	Листов
	П	30	94

выпуск 13.11.2026 № c38d47cb31 · стр. 30 из 94

Стена А (М 1:20)

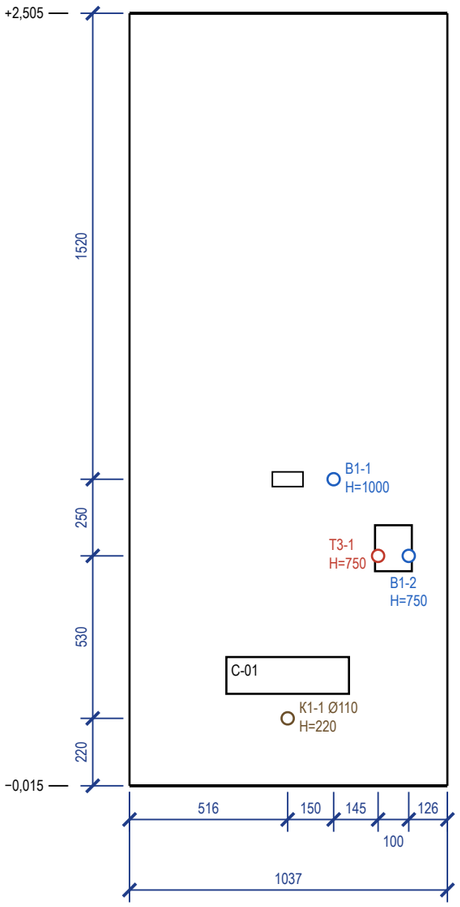

Стена Г (М 1:20)

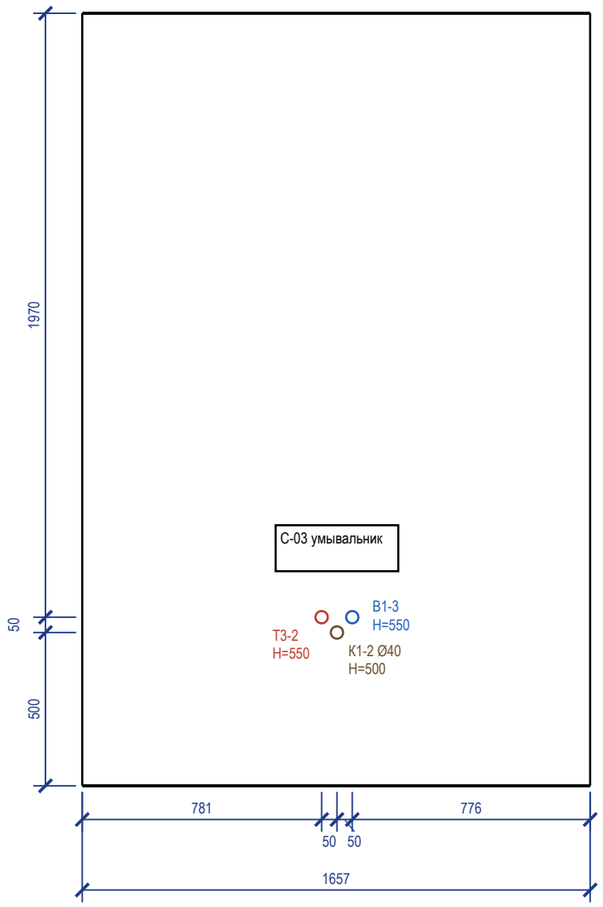

Ведомость привязок выводов (от чистого пола и угла)

Код	Прибор	Ø	H, мм	Привязка, мм
B1-1	C-01 унитаз подвесной	½"	1000	ст. А: 666 от лев. угла
K1-1	C-01 унитаз подвесной	Ø110	220	ст. А: 516 от лев. угла
B1-2	C-02 гигиенический душ	½"	750	ст. А: 911 от лев. угла
T3-1	C-02 гигиенический душ	½"	750	ст. А: 811 от лев. угла
B1-3	C-03 умывальник	½"	550	ст. Г: 881 от лев. угла
T3-2	C-03 умывальник	½"	550	ст. Г: 781 от лев. угла
K1-2	C-03 умывальник	Ø40	500	ст. Г: 831 от лев. угла

Условные обозначения

- вывод B1 (код — в ведомости привязок)
- вывод T3 (код — в ведомости привязок)
- вывод K1 (код — в ведомости привязок)
- сантехприбор по расстановке (габарит модели)
- дверной проём; окно — сплошной контур
- кнопка смыва инсталляции (H — по данным прибора)

Примечания

1. Габариты и высоты приборов, межосевые смесителей и места кранов — по паспортам выбранных приборов, сверяются до разметки стен.
2. Высоты H — от чистого пола помещения, мм; отметка чистого пола и потолка — у левого края вида (от ±0,000 объекта). Привязки — от левого чистового угла вида (облицовка стен вычтена), как на развёртках стен.
3. Кнопка смыва C-01 — H=1000 (по данным прибора).
4. Ревизионные люки (арматура и ревизии у C-01, C-02 300×400, стена А у C-01, предложение): привязка к углу — по раскладке плитки, подтверждается обмером.
5. Ревизионные люки к арматуре и ревизиям в данных не заданы: место и размер не определены (записи реестра нет).
6. Расчёт систем водоснабжения и канализации и подбор оборудования выполняет проектная организация; лист задаёт места и высоты выводов.

	Лист	№ док.	Подпись	Дата
Дизайнер	Кырлан А.С.			13.11.26
Проверил				
Н. контр.				
Утв.				


Проект: Квартира 68 м², элитный модерн — **М 1:20**

Развёртки мокрых зон: выводы ВК. Санузел


Стадия	Лист	Листов
П	31	94

выпуск 13.11.2026 № c38d47cb31 · стр. 31 из 94


Стена А (М 1:20)

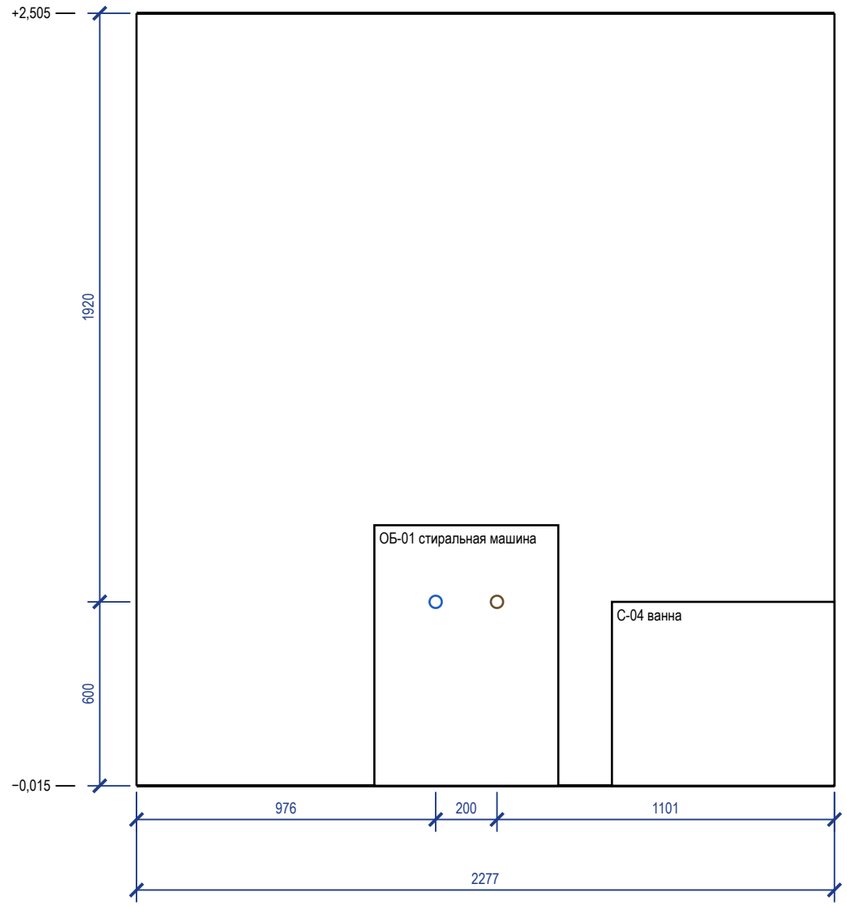

Стена Б (М 1:20)

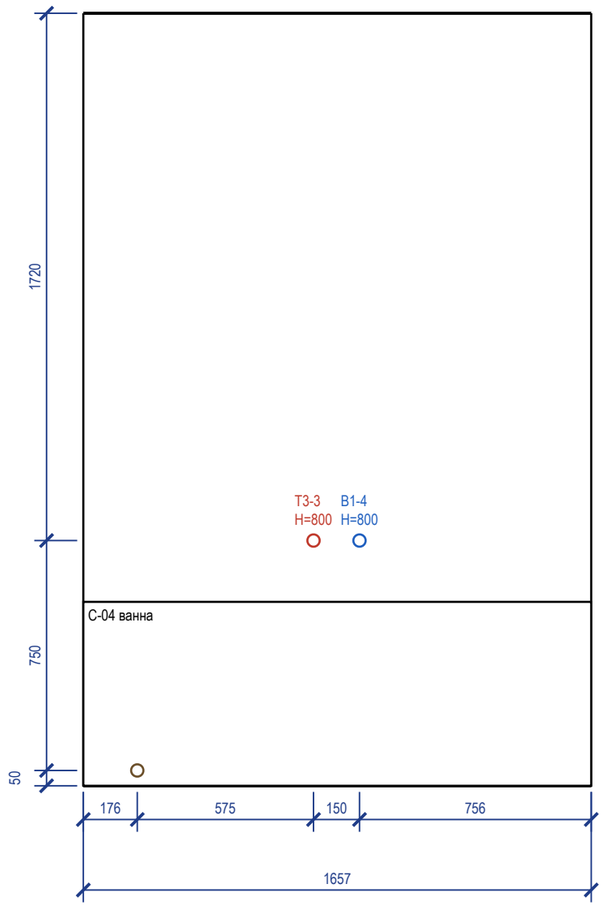

Стена Г (М 1:20)

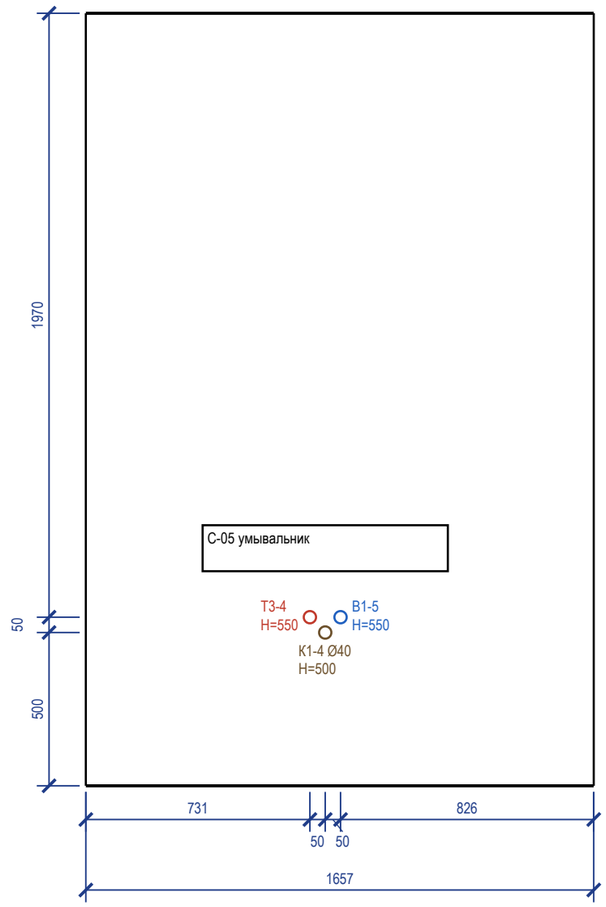

Ведомость привязок выводов (от чистого пола и угла)

Код	Прибор	Ø	H, мм	Привязка, мм
В1-6	ОБ-01 стиральная машина	½"	600	ст. А: 976 от лев. угла
К1-5	ОБ-01 стиральная машина	Ø40	600	ст. А: 1176 от лев. угла
В1-4	С-04 ванна	½"	800	ст. Б: 901 от лев. угла
Т3-3	С-04 ванна	½"	800	ст. Б: 751 от лев. угла

Ведомость привязок (продолжение)

Код	Прибор	Ø	H, мм	Привязка, мм
К1-3	С-04 ванна	Ø50	50	ст. Б: 176 от лев. угла
В1-5	С-05 умывальник	½"	550	ст. Г: 831 от лев. угла
Т3-4	С-05 умывальник	½"	550	ст. Г: 731 от лев. угла
К1-4	С-05 умывальник	Ø40	500	ст. Г: 781 от лев. угла

Условные обозначения

- вывод В1 (код — в ведомости привязок)
- вывод Т3 (код — в ведомости привязок)
- вывод К1 (код — в ведомости привязок)
- сантехприбор по расстановке (габарит модели)
- дверной проём; окно — сплошной контур

Примечания

1. Габариты и высоты приборов, межосевые смесителей и места кранов — по паспортам выбранных приборов, сверяются до разметки стен.
2. Высоты H — от чистого пола помещения, мм; отметка чистого пола и потолка — у левого края вида (от ±0,000 объекта). Привязки — от левого чистового угла вида (облицовка стен вычтена), как на развёртках стен.
3. Стояки в помещении: Ст К1-1 Ø110, Ст В1-2 Ø32, Ст Т3-3 Ø32 — положение на плане выводов; выводы подключаются к ним по схеме разводки.
4. Ревизионные люки (С-04 400×300, стена Б, предложение; узел ввода воды (электрокраны ЭК-1, ЭК-2, счётчики, коллектор) 400×600, стена Б у С-04, предложение): привязка к углу — по раскладке плитки, подтверждается обмером.
5. Ревизионные люки к арматуре и ревизиям в данных не заданы: место и размер не определены (записи реестра нет).
6. Часть подписей выводов не уместилась у знака: коды и высоты — в ведомости привязок.
7. Стены В: выводов В1, Т3, К1 нет — развёртка не строится (иначе лист-продолжение); приборы и проёмы этих стен — на плане выводов и развёртках стен чертёжника.
8. Расчёт систем водоснабжения и канализации и подбор оборудования выполняет проектная организация; лист задаёт места и высоты выводов.

	Лист	№ док.	Подпись	Дата
Дизайнер	Кырлан А.С.			13.11.26
Проверил				
Н. контр.				
Утв.				


Проект: Квартира 68 м², элитный модерн — **М 1:20**

Развёртки мокрых зон: выводы ВК. Ванная

Стадия	Лист	Листов
П	32	94

выпуск 13.11.2026 № c38d47cb31 · стр. 32 из 94

Стена А (М 1:20)

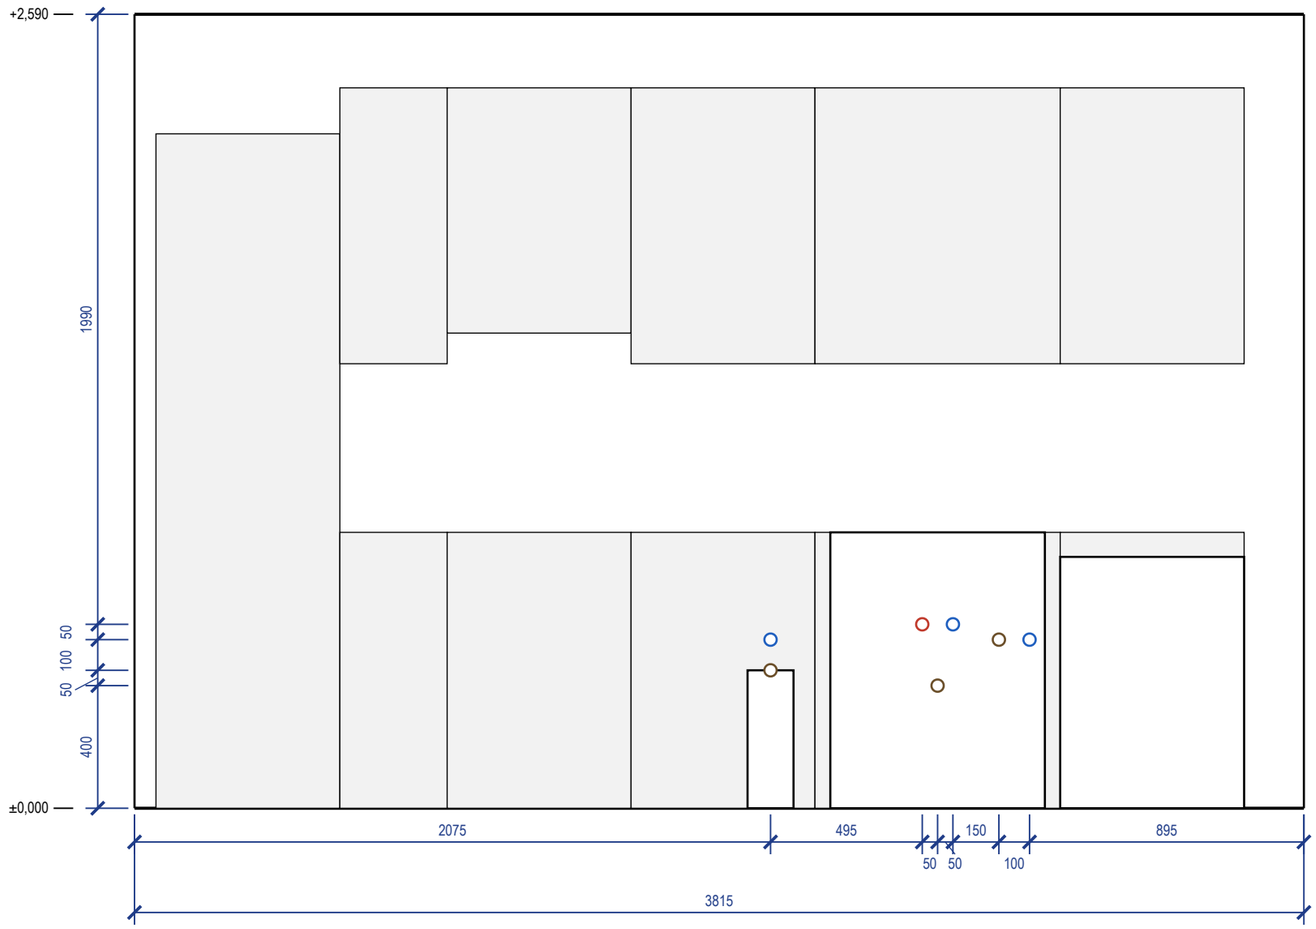

Ведомость привязок выводов (от чистого пола и угла)

Код	Прибор	Ø	H, мм	Привязка, мм
В1-7	С-06 мойка кухонная	½"	600	ст. А: 2670 от лев. угла
Т3-5	С-06 мойка кухонная	½"	600	ст. А: 2570 от лев. угла
К1-6	С-06 мойка кухонная	Ø50	400	ст. А: 2620 от лев. угла
В1-8	ОБ-02 посудомоечная машина	½"	550	ст. А: 2920 от лев. угла

Ведомость привязок (продолжение)

Код	Прибор	Ø	H, мм	Привязка, мм
К1-7	ОБ-02 посудомоечная машина	Ø40	550	ст. А: 2820 от лев. угла
В1-9	С-07 фильтр обратного осмоса	½"	550	ст. А: 2075 от лев. угла
К1-8	С-07 фильтр обратного осмоса	Ø40	450	ст. А: 2075 от лев. угла

Условные обозначения

- вывод В1 (код — в ведомости привязок)
- вывод Т3 (код — в ведомости привязок)
- вывод К1 (код — в ведомости привязок)
- сантехприбор по расстановке (габарит модели)
- дверной проём; окно — сплошной контур

Примечания

1. Габариты и высоты приборов, межосевые смесителей и места кранов — по паспортам выбранных приборов, сверяются до разметки стен.
2. Высоты H — от чистого пола помещения, мм; отметка чистого пола и потолка — у левого края вида (от ±0,000 объекта). Привязки — от левого чистового угла вида (облицовка стен вычтена), как на развёртках стен.
3. Ревизионные люки (арматура и ревизии у С-06, ОБ-02, С-07 300×400, стена А у С-06, предложение): привязка к углу — по раскладке плитки, подтверждается обмером.
4. Ревизионные люки к арматуре и ревизиям в данных не заданы: место и размер не определены (записи реестра нет).
5. Мойка, ПММ и фильтр — выводы в шкафу мойки; диаметры и положение сифона и кранов сверить по паспортам приборов и чертежам модуля.
6. Часть подписей выводов не уместилась у знака: коды и высоты — в ведомости привязок.
7. Расчёт систем водоснабжения и канализации и подбор оборудования выполняет проектная организация; лист задаёт места и высоты выводов.

	Лист	№ док.	Подпись	Дата	Проект: Квартира 68 м², элитный модерн			М 1:20
Дизайнер	Кырлан А.С.			13.11.26	Развёртки мокрых зон: выводы ВК. Кухня-столовая	Стадия	Лист	Листов
Проверил						П	33	94
Н. контр.								
Утв.								

выпуск 13.11.2026 № c38d47cb31 · стр. 33 из 94

Поз.	Наименование и техническая характеристика	Тип, марка, обозначение документа	Код продукции	Поставщик	Ед. изм.	Кол.	Масса 1 ед., кг	Примечание
	Санитарные приборы							
1	Ванна встраиваемая акриловая 1700×750 мм, с каркасом, экраном и отверстием слив-перелив	акриловая 1700×750, смеситель настенный		выбор заказчика	шт	1		С-04
2	Унитаз подвесной безободковый, с сиденьем микролифт, крепёж и звукоизолирующая прокладка	инсталляция 1120 + подвесной унитаз		выбор заказчика	шт	1		С-01
3	Инсталляция для подвесного унитаза: рама высотой 1120 мм, бачок, клавиша смыва (ось клавиши 1050 мм от чистого пола)	аналог		выбор заказчика	шт	1		С-01; короб ГКЛВ
4	Умывальник подвесной 400×280 мм, с отверстием под смеситель и переливом	раковина подвесная 400 × 280, смеситель на раковине аналог по характеристикам		выбор заказчика	шт	1		С-03
5	Раковина накладная 800×500 мм, на столешницу тумбы, с переливом	раковина-столешница на подвесной тумбе 800 × 500, смеситель на раковине аналог по характеристикам		выбор заказчика	шт	1		С-05
6	Гигиенический душ: ручная лейка с кнопкой-запорником, шланг 1,25 м, настенный держатель	аналог		выбор заказчика	шт	1		С-02
7	Мойка врезная, нержавеющая сталь 700×480 мм, с переливом	аналог		с кухонной мебелью	шт	1		С-06
8	Фильтр обратного осмоса под мойку, с отдельным краном и врезкой дренажа	аналог		выбор заказчика	шт	1		С-07
	Смесители, сифоны и арматура приборов							
9	Смеситель для ванны настенный однорычажный, межосевое 150 мм, с душевым набором (лейка, шланг, держатель)	аналог		выбор заказчика	шт	1		С-04
10	Смеситель для умывальника однорычажный, с донным клапаном	аналог		выбор заказчика	шт	1		С-03
11	Смеситель для накладной раковины однорычажный, высокий излив, с донным клапаном	аналог		выбор заказчика	шт	1		С-05
12	Смеситель кухонный однорычажный, высокий излив	аналог		выбор заказчика	шт	1		С-06
13	Смеситель для гигиенического душа скрытого монтажа однорычажный: встраиваемая часть, накладная панель с рычагом, вывод на лейку; встраиваемая часть — до плитки	аналог		выбор заказчика	шт	1		С-02; выводы В1, Т3 — по листу выводов
14	Обвязка ванны слив-перелив Ø40/50 с сифоном	аналог		выбор заказчика	шт	1		С-04
15	Сифон для умывальника бутылочный Ø32/40–50, с гофрой к выпуску	аналог		выбор заказчика	шт	2		С-03, С-05
16	Сифон для мойки Ø40/50	аналог		выбор заказчика	шт	1		С-06
17	Сифон для посудомоечной машины с обратным клапаном, на выводе слива Ø40	аналог		выбор заказчика	шт	1		ОБ-02
18	Сифон для стиральной машины встраиваемый в стену Ø50, с обратным клапаном	аналог		выбор заказчика	шт	1		ОБ-01
19	Кран угловой ½"×½" с гибкой подводкой 40 см (умывальники, мойка)	аналог		выбор заказчика	шт	6		по 2 на прибор
20	Кран шаровой угловой ½"×¾" для подключения стиральной и посудомоечной машины	аналог		выбор заказчика	шт	2		ОБ-01, ОБ-02
	Трубопроводы							
21	Труба полипропиленовая PP-R PN20 Ø20×3,4 (В1)	ГОСТ 32415-2013		выбор заказчика	м	17,5	0,17	9,8 + 6,0 + 10 %
22	Труба PP-R, армированная стекловолокном, PN20 Ø20×2,8 (Т3)	ГОСТ 32415-2013		выбор заказчика	м	14	0,15	9,1 + 3,3 + 10 %
23	Труба канализационная ПП Ø40 (К1)	ГОСТ 32414-2013		выбор заказчика	м	6,5		3,0 + 2,6 + 10 %
24	Труба канализационная ПП Ø50 (К1)	ГОСТ 32414-2013		выбор заказчика	м	8		6,8 + 0,5 + 10 %
25	Труба канализационная ПП Ø110 (К1)	ГОСТ 32414-2013		выбор заказчика	м	2		1,3 + 0,2 + 10 %
	Фасонные части и выводы							
26	Отвод канализационный ПП 45° Ø40	ГОСТ 32414-2013		выбор заказчика	шт	10		2 шт. на поворот
27	Отвод канализационный ПП 45° Ø50	ГОСТ 32414-2013		выбор заказчика	шт	12		2 шт. на поворот
28	Отвод канализационный ПП 45° Ø110	ГОСТ 32414-2013		выбор заказчика	шт	6		2 шт. на поворот
29	Тройник канализационный ПП 45° (врезки ветвей)	ГОСТ 32414-2013		выбор заказчика	шт	7		
30	Ревизия канализационная ПП (после поворота трассы)	ГОСТ 32414-2013		выбор заказчика	шт	8		доступ сохранить
31	Фитинги PP-R Ø20: тройники, угольники 90° (ветви и повороты В1, Т3)	ГОСТ 32415-2013		выбор заказчика	шт	23		
32	Водорозетка PP-R Ø20×½" настенная, с креплением	ГОСТ 32415-2013		выбор заказчика	шт	14		коды — лист выводов
	Узлы ввода, люки, короба							
33	Кран шаровой латунный Ду15 PN16 (отключение ввода)	аналог		выбор заказчика	шт	2		Ст В1-2, Ст Т3-3
34	Фильтр сетчатый косой Ду15	аналог		выбор заказчика	шт	2		
35	Счётчик воды крыльчатый Ду15 (ХВ, ГВ), с поверкой	аналог		выбор заказчика	шт	2		пломба УК
36	Клапан обратный Ду15	аналог		выбор заказчика	шт	2		
37	Люк ревизионный нажимной под плитку 300×400 мм	аналог		выбор заказчика	шт	4		к стоякам и арматуре
38	Звукоизоляция стояка К1 в коробе: рулонный звукоизоляционный материал ≥ 10 мм, обмотка стояка на высоту этажа	аналог		выбор заказчика	м	2,7		Ст К1-1
39	Короб К1 над полом: профиль ПН/ПС, ГКЛВ 12,5 мм под плитку	аналог		выбор заказчика	м	2,3		сечение — лист разводки

Примечания


1. Форма 1 ГОСТ 21.110-2013, ширины граф изменены по п. 4.1. «Аналог» — аналог по характеристикам: модели внести до черновых работ, привязки выводов сверить по паспортам.
2. Бытовая техника не входит (показана арматура подключения), мойка — в комплекте кухни (марка — модуля кухни, как у столяра). Длины труб — трасса листа разводки + подъёмы + 10 %.
3. Стояк К1 в коробе — звукоизоляция стояка в коробе без жёсткого контакта короба с трубой.
4. Расчёт систем водоснабжения и канализации, диаметры магистралей и подбор оборудования выполняет проектная организация.


	Лист	№ док.	Подпись	Дата
Дизайнер	Кырлан А.С.			13.11.26
Проверил				
Н. контр.				
Утв.				

Проект: Квартира 68 м², элитный модерн

Спецификация сантехнического оборудования	Стадия	Лист	Листов
	П	34	94

выпуск 13.11.2026 № c38d47cb31 · стр. 34 из 94

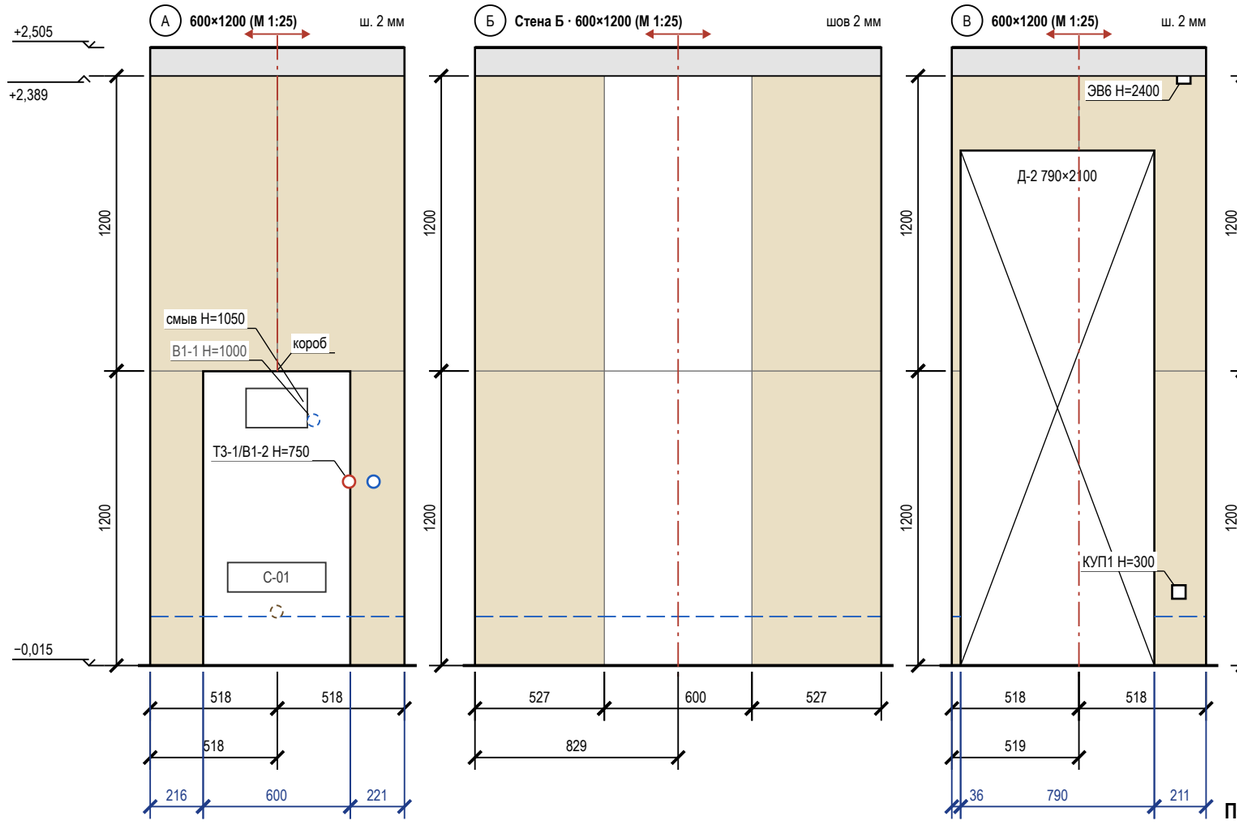

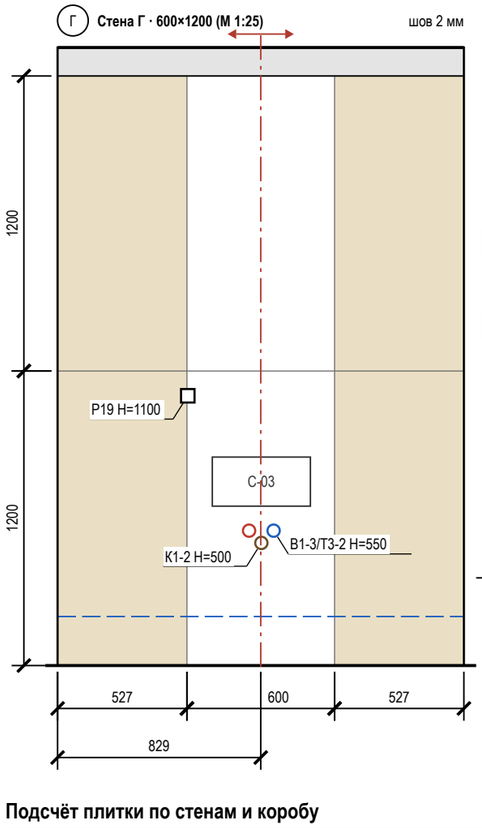

Условные обозначения

- плитка целая; тонкая линия — шов
- плитка с подрезкой (размер — на цепочке)
- ось старта; стрелки — направление укладки
- верх гидроизоляции: 200 от ЧП, в мокрой зоне — «до …»
- проём — не облицовывается
- сантехприбор: габарит, высота по практике
- короб инсталляции, в нём кнопка смыва 250×160
- вывод В1 (код — в ведомости привязок)
- вывод Т3 (код — в ведомости привязок)
- вывод К1 (код — в ведомости привязок)
- вывод за прибором / в коробе (не на сетке)
- электроточка: марка и Н — по листам ЭОМ
- отметка уровня, м: ±0,000 — чистый пол жилых помещений
- низ потолка; серая полоса — стена без плитки
- А обозначение стены А–Г (как на развёртках)

Подсчёт плитки по стенам и коробу

Поверхность	L × H, мм	S, м²	Целых	Подр.	С запасом	Подрезки: край / верх, мм
стена А	1037 × 2404	1,89	0	4	5	518 / 518; целый ряд
короб (ст. А)	600×1200×250	1,47	1	3	5	лицо 600; бок. 250
стена Б	1657 × 2404	4,10	2	4	7	527 / 527; целый ряд
стена В	1037 × 2404	0,95	0	4	5	518 / 518; целый ряд
стена Г	1657 × 2404	4,10	2	4	7	527 / 527; целый ряд
Итого		**12,51**	**5**	**19**	**29**	

Сдвиг точек под раскладку


Точка (ВК, ЭОМ)	Стена	Проект: от угла / Н	Под раскладку: от угла / Н	Сдвиг, мм
ЭВ6	В	946 / 2400	819 / 2400	−127 в центр плитки
КУП1	В	926 / 300	819 / 300	−107 в центр плитки

Примечания

1. Вид изнутри, стены по часовой стрелке А → Г. Высоты — от чистого пола (−0,015), отметки — от ±0,000. Раскладка от чистовых размеров (штукатурка 10 + клей 5 + плитка 9 мм), подрезки чистые; старт — от оси стены, ряды от пола целыми.
2. Верх плитки +2,389, потолок +2,505, зазор 116 мм: потолок ГКЛ опустить до +2,392 (шов 3 мм, герметик) — согласовать с монтажником ГКЛ; иначе профиль-окантовка, полосу окрасить в цвет потолка. Подрезной ряд 111 мм не делать.
3. Точки из таблицы сдвигов переносятся до черновой разводки (ЭОМ — по тем же числам).
4. Выводы ВК стоят по оси прибора и с прибором не двигаются — привязки по «Плану выводов сантехники» без сдвига; вне сетки (Т3-1/В1-2) — отверстие в плитке коронкой по той же привязке, плитку не сдвигать.
5. За приборами и в коробе (В1-1, К1-1) — штриховым кольцом.
6. Гидроизоляция: 200 мм от ЧП по периметру; углы — лентой; акт скрытых работ, пролив.
7. Короб 600×1200×250: лицо 600 мм от оси кнопки смыва, боковины, полка; углы — запил 45° или профиль; за коробом плитку не кладут.

	Лист	№ док.	Подпись	Дата	Проект: Квартира 68 м², элитный модерн			М 1:25
Дизайнер	Кырлан А.С.			13.11.26	Раскладка плитки. Санузел. Развёртки стен	Стадия	Лист	Листов
Проверил						П	35	94
Н. контр.								
Утв.								

выпуск 13.11.2026 № c38d47cb31 · стр. 35 из 94

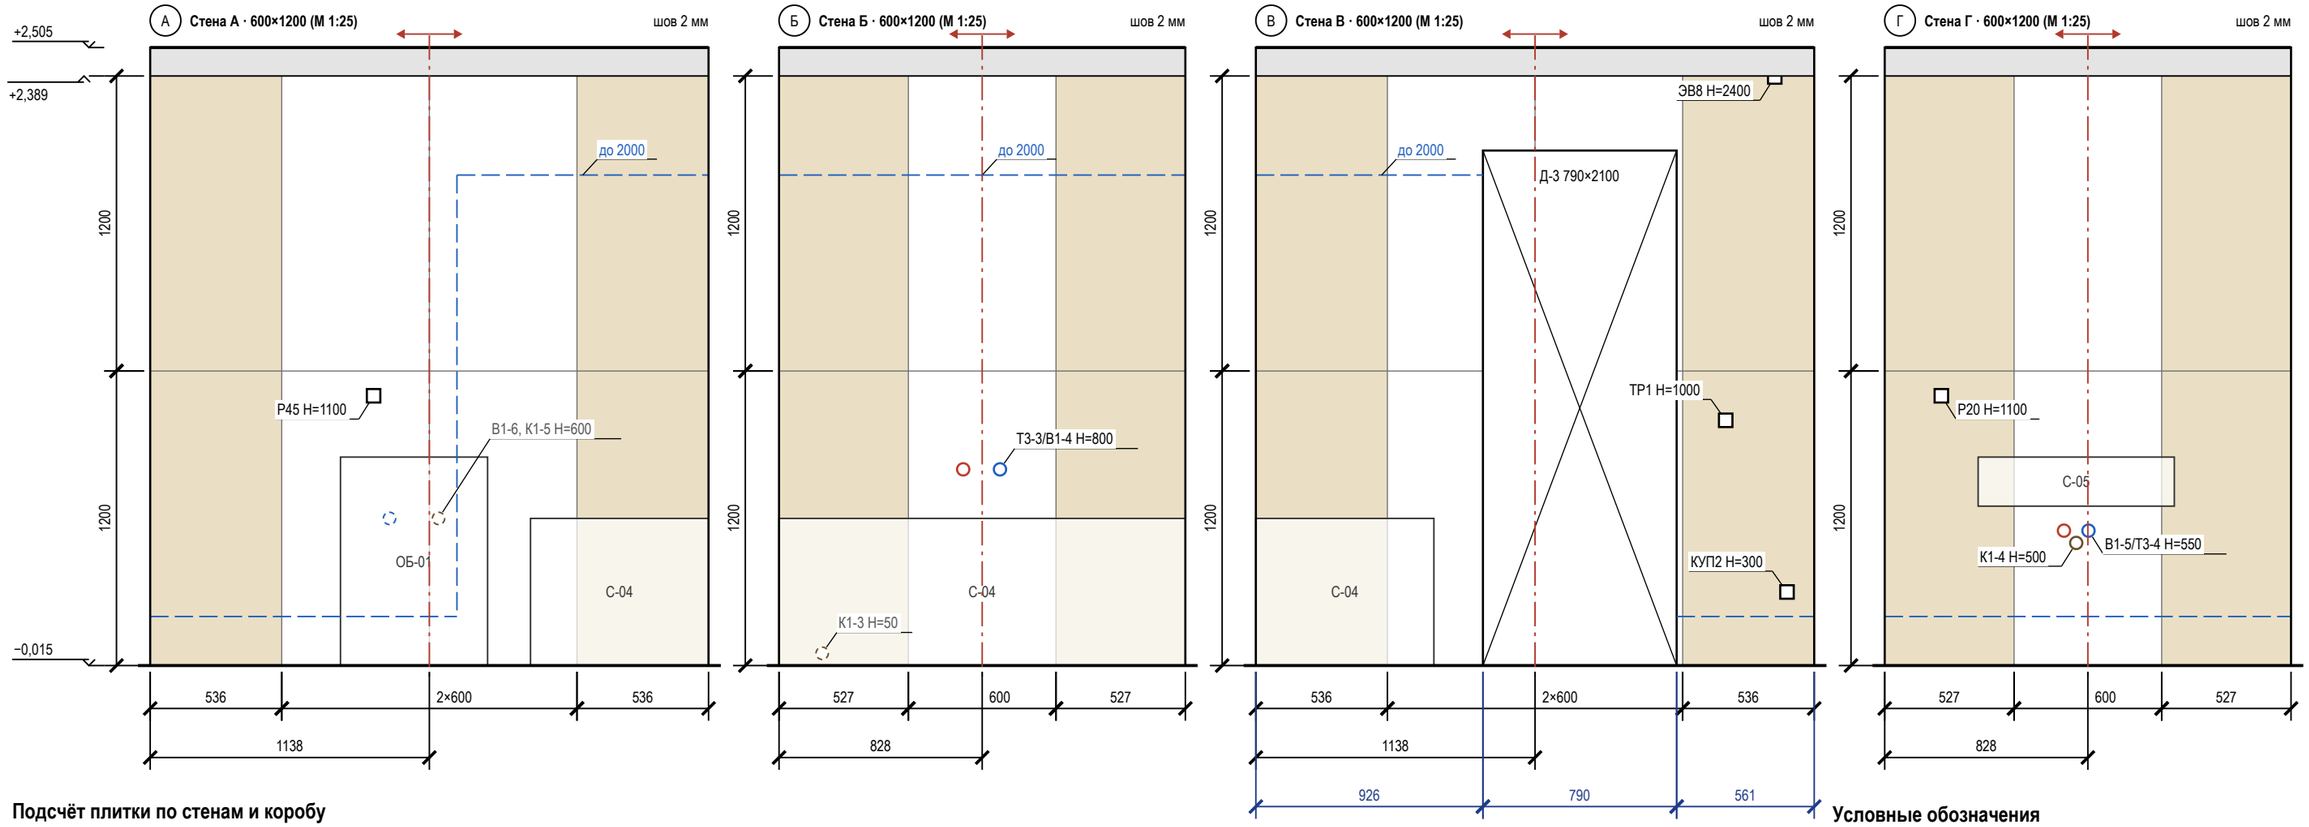

Подсчёт плитки по стенам и коробу

Поверхность	L × H, мм	S, м²	Целых	Подр.	С запасом	Подрезки: край / верх, мм
стена А	2277 × 2404	5,59	4	4	9	536 / 536; целый ряд
стена Б	1657 × 2404	4,10	2	4	7	527 / 527; целый ряд
стена В	2277 × 2404	3,93	0	8	9	536 / 536; целый ряд
стена Г	1657 × 2404	4,10	2	4	7	527 / 527; целый ряд
Итого		**17,72**	**8**	**20**	**32**	

Сдвиг точек под раскладку

Точка (ВК, ЭОМ)	Стена	Проект: от угла / Н	Под раскладку: от угла / Н	Сдвиг, мм
Р45	А	911 / 1100	838 / 1100	−73 в центр плитки
ЭВ8	В	2116 / 2400	2041 / 2400	−75 в центр плитки
КУП2	В	2166 / 300	2041 / 300	−125 в центр плитки
ТР1	В	1916 / 1000	2041 / 1000	+125 в центр плитки

Примечания

1. Вид изнутри, стены по часовой стрелке А → Г. Высоты — от чистого пола (−0,015), отметки — от ±0,000. Раскладка от чистовых размеров (штукатурка 10 + клей 5 + плитка 9 мм), подрезки чистые; старт — от оси стены, ряды от пола целыми.
2. Верх плитки +2,389, потолок +2,505, зазор 116 мм: потолок ГКЛ опустить до +2,392 (шов 3 мм, герметик) — согласовать с монтажником ГКЛ; иначе профиль-окантовка, полосу окрасить в цвет потолка. Подрезной ряд 111 мм не делать.
3. Точки из таблицы сдвигов переносятся до черновой разводки (ЭОМ — по тем же числам).
4. Выводы ВК стоят по оси прибора и с прибором не двигаются — привязки по «Плану выводов сантехники» без сдвига; вне сетки (В1-5/Т3-4, К1-4) — отверстие в плитке коронкой по той же привязке, плитку не сдвигать.
5. За приборами и в коробе (В1-6, К1-5, К1-3) — штриховым кольцом.
6. Гидроизоляция: 200 мм от ЧП по периметру; над ванной — до 2000 и 300 мм за борт (СП 29.13330.2011, п. 7.2 — на высоту замачивания); углы — лентой; акт скрытых работ, пролив.

Условные обозначения

- плитка целая; тонкая линия — шов
- плитка с подрезкой (размер — на цепочке)
- ось старта; стрелки — направление укладки
- верх гидроизоляции: 200 от ЧП, в мокрой зоне — «до …»
- проём — не облицовывается
- сантехприбор: габарит, высота по практике
- вывод В1 (код — в ведомости привязок)
- вывод Т3 (код — в ведомости привязок)
- вывод К1 (код — в ведомости привязок)
- вывод за прибором / в коробе (не на сетке)
- электроточка: марка и Н — по листам ЭОМ
- отметка уровня, м: ±0,000 — чистый пол жилых помещений
- низ потолка; серая полоса — стена без плитки
- А — обозначение стены А–Г (как на развёртках)


	Лист	№ док.	Подпись	Дата
Дизайнер	Кырлан А.С.			13.11.26
Проверил				
Н. контр.				
Утв.				

Проект: Квартира 68 м², элитный модерн — **М 1:25**

Раскладка плитки. Ванная. Развёртки стен

Стадия	Лист	Листов
П	36	94

выпуск 13.11.2026 № c38d47cb31 · стр. 36 из 94

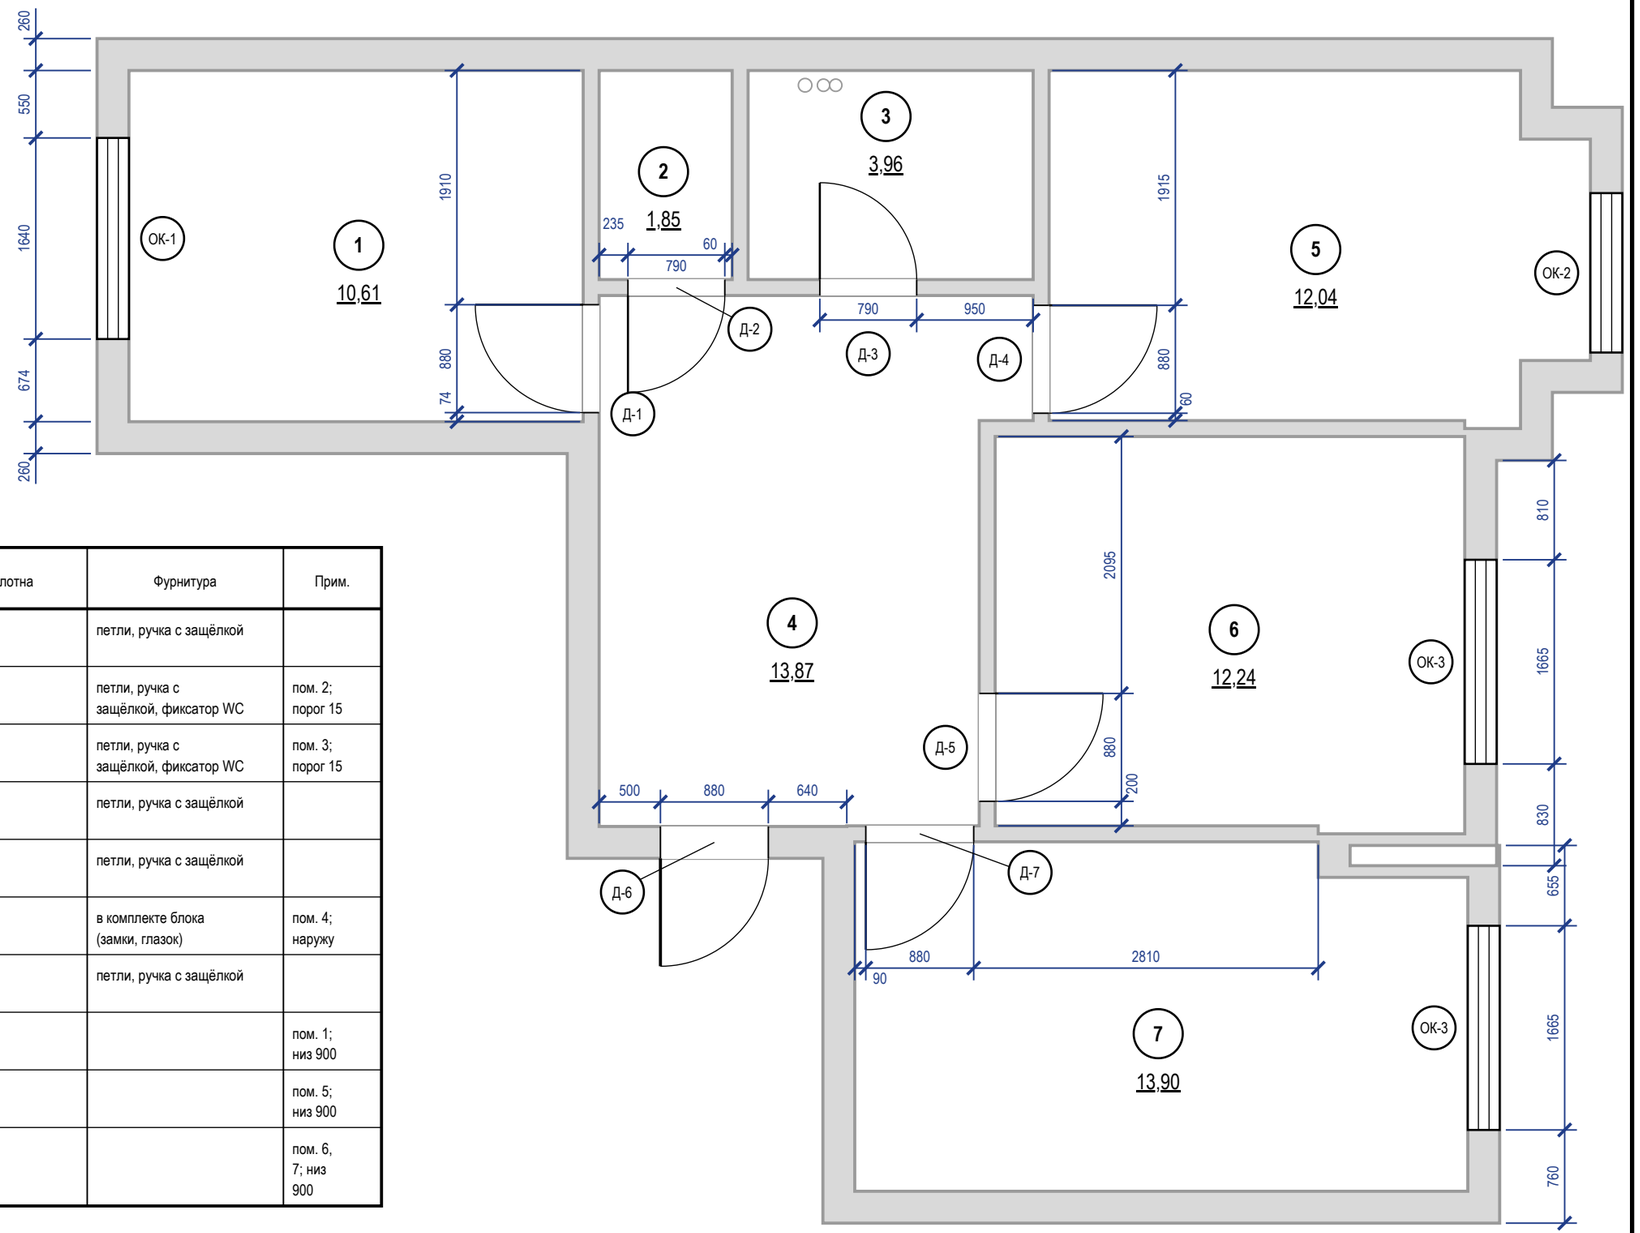

Ведомость заполнения проёмов


Марка	Наименование, обозначение	Проём ш×в, мм	Полотно (расч.)	Кол.	Откр.	Отделка полотна	Фурнитура	Прим.
Д-1	Блок дверной внутренний, ГОСТ 475-2016	880×2100	800×2000	1	Л		петли, ручка с защёлкой	
Д-2	Блок дверной внутренний, ГОСТ 475-2016	790×2100	700×2000	1	Л		петли, ручка с защёлкой, фиксатор WC	пом. 2; порог 15
Д-3	Блок дверной внутренний, ГОСТ 475-2016	790×2100	700×2000	1	П		петли, ручка с защёлкой, фиксатор WC	пом. 3; порог 15
Д-4	Блок дверной внутренний, ГОСТ 475-2016	880×2100	800×2000	1	П		петли, ручка с защёлкой	
Д-5	Блок дверной внутренний, ГОСТ 475-2016	880×2100	800×2000	1	П		петли, ручка с защёлкой	
Д-6	Блок дверной входной, ГОСТ 31173-2016	880×2100	блок задать	1	Л	в комплекте блока	в комплекте блока (замки, глазок)	пом. 4; наружу
Д-7	Блок дверной внутренний, ГОСТ 475-2016	880×2100	800×2000	1	Л		петли, ручка с защёлкой	
ОК-1	Блок оконный, ГОСТ 23166-2021	1640×1500		1				пом. 1; низ 900
ОК-2	Блок оконный, ГОСТ 23166-2021	1300×1500		1				пом. 5; низ 900
ОК-3	Блок оконный, ГОСТ 23166-2021	1665×1500		2				пом. 6, 7; низ 900

Примечания

1. Размеры проёмов и привязки — в миллиметрах от чистых граней стен до отделки; привязка — от угла того помещения, со стороны которого стоит размер. Размер проёма — ширина × высота от чистого пола 0,000. Размеры на плане — проёмов, не полотен: полотно — в ведомости, коробка — по системе.
2. Марки в кружках — типы заполнения проёмов (ГОСТ 21.501-2018, п. 5.3.2); одна марка — один типоразмер; количество сверено с планом.
3. Открывание: Л — петли слева, П — справа, если смотреть со стороны, куда открывается полотно (на себя).
4. Дверные блоки обычного монтажа (Д-1…Д-5, Д-7) заказывать после чистовой стяжки и штукатурки, проёмы перемерить; монтажный зазор коробки 10–15 мм на сторону, откос от угла помещения до коробки не менее 50 мм.
5. Полотно «расч.» — по проёму с запасом по каталогам, заказ — по таблице проёмов модели; Д-1…Д-5, Д-7: проём 2100, а под полотно 2000 по каталогам нужен 2040–2080, под 2100 — 2140–2180: высоту проёма — по модели; Д-6: входной блок по ГОСТ 31173-2016 — задать при выборе блока.
6. Экспликация помещений — лист 14; в марках помещений — номер и площадь, м².

	Лист	№ док.	Подпись	Дата	Проект: Квартира 68 м², элитный модерн	М 1:50		
Дизайнер	Кырлан А.С.			13.11.26	План размещения дверей	Стадия	Лист	Листов
Проверил						П	37	94
Н. контр.								
Утв.								

выпуск 13.11.2026 · c38d47cb31 · стр. 37 из 94

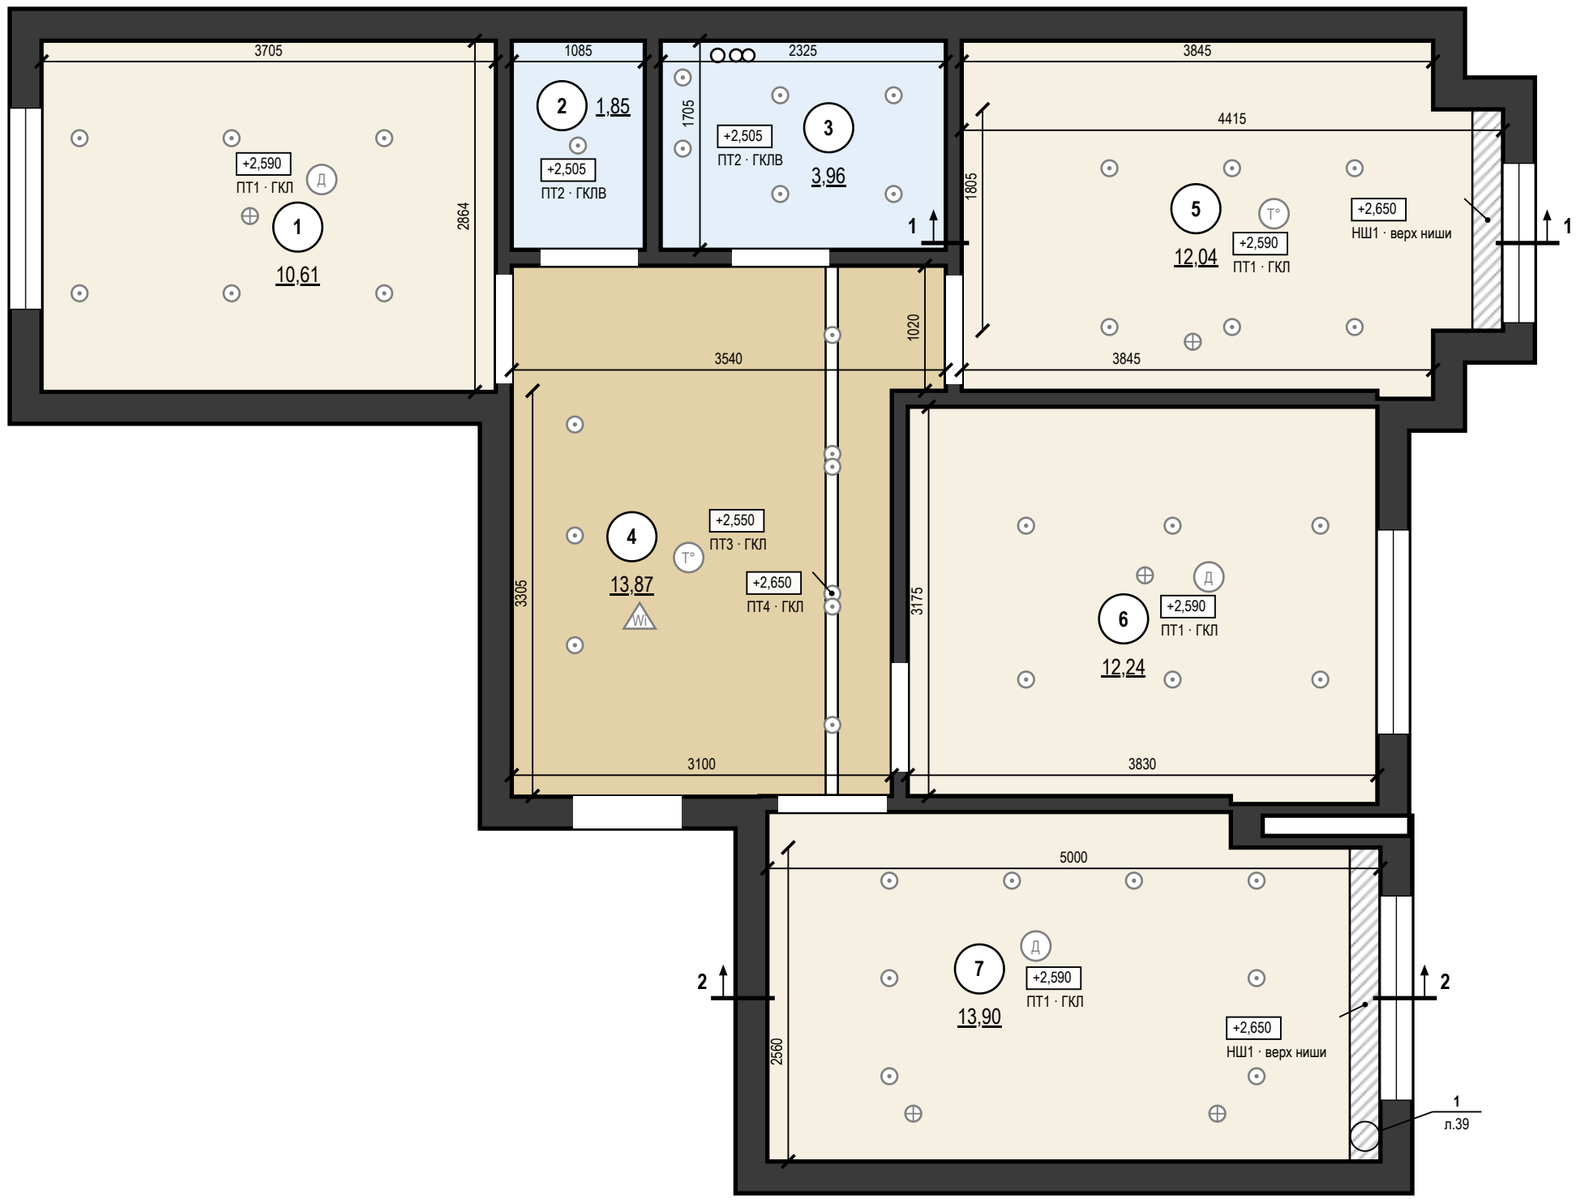

Ведомость потолков

Пом.	Марка	Конструкция	Низ / верх ниши	S, м²	Q
1	ПТ1	ГКЛ П113	+2,590	10,61	Q3
2	ПТ2	ГКЛВ П113	+2,505	1,85	Q3
3	ПТ2	То же	+2,505	3,96	Q3
4	ПТ3	ГКЛ П113	+2,550	13,44	Q3
4	ПТ4	Существующий потолок	+2,650	0,43	
5	ПТ1	ГКЛ П113	+2,590	11,59	Q3
5	НШ1	ниша под шторы 250×60	+2,650	0,45	
6	ПТ1	ГКЛ П113	+2,590	12,24	Q3
7	ПТ1	То же	+2,590	13,26	Q3
7	НШ1	ниша под шторы 250×60	+2,650	0,64	
		Итого		**68,47**	

Ведомость вырезов и закладных в потолке

Марка	Устройство	Кол.	Пом.
	Светильник встраиваемый (марки — план освещения)	42	1, 2, 3, 4, 5, 6, 7
	Светильник подвесной (марки — план освещения)	5	1, 5, 6, 7
ИП1, ИП4, ИП5	Извещатель дымовой	3	1, 6, 7
ИП2, ИП3	Извещатель тепловой	2	4, 5
АР1	Точка доступа Wi-Fi, PoE	1	4

1. За отметку ±0,000 принят уровень чистого пола сухих помещений (готовое покрытие), а не существующего пола; пол пом. 2, 3 — −0,015; верх плиты перекрытия −0,064 — расчётный по пирогу пола, не замерен; существующий пол снимается до плиты, его отметка не замерена. Отметки в прямоугольниках — низ потолка; низ перекрытия +2,650. Марка потолка — одна конструкция и отметка на весь альбом.
2. Размеры помещений в свету (ширина × длина, мм), не поместившиеся на плане: пом. 2 — 1085 × 1705; пом. 4 — 3540 × 1020, 3100 × 3305, 2020 × 5; пом. 6 — 3830 × 3175, 1195 × 65; пом. 7 — 3780 × 290, 5000 × 2560.
3. Потолки ГКЛ — каркасная система П113: подвесы через 1000 (с запасом: СП 163, табл. 14 — до 1100 при 0,15 кН/м²), несущие профили через 500, основные через 1200 мм; листы — поперёк несущих профилей. В помещениях 2, 3 — ГКЛВ на оцинкованном каркасе.
4. Ниши под шторы 250×60 мм — на всю длину стены с окном; карниз — на закладной до обшивки (узел 1, лист 39).
5. Примыкание к стенам: теневой шов 15 мм, техзазор 3 мм — пом. 1, 4, 5, 6, 7, по стенам, выровненным штукатуркой (узел 1); пом. 2, 3 — разделительная лента.
6. Светильники и потолочные устройства — подложка с планов освещения, слаботочных систем и вентиляции (положение — по ним); вырезы и закладные по ведомости на листе, до обшивки; отверстия не совмещать с профилями, глубина корпуса светильника до 50 мм.
7. Разрезы 1–1, 2–2 — на листе 39; высоты мебели и дверных блоков сверены с низом потолка в разрезах.
8. Шпаклевание ГКЛ и условия приёмки — Q3: рассеянный дневной свет, осмотр с 2 м; боковой свет не оценивается.
9. Сечения потолков М 1:10: пом. 5 — 5.1, 5.2 (лист 40); пом. 7 — 5.1, 5.2 (лист 40).


	Лист	№ док.	Подпись	Дата	Проект: Квартира 68 м², элитный модерн			М 1:50
Дизайнер	Кырлан А.С.			13.11.26	План потолков	Стадия	Лист	Листов
Проверил						П	38	94
Н. контр.								
Утв.								

Примечания

выпуск 13.11.2026 № c38d47cb31 · стр. 38 из 94


Разрез 1–1 (М 1:40)

Пом. 5 Кухня-столовая; линия разреза — план потолков, лист 38

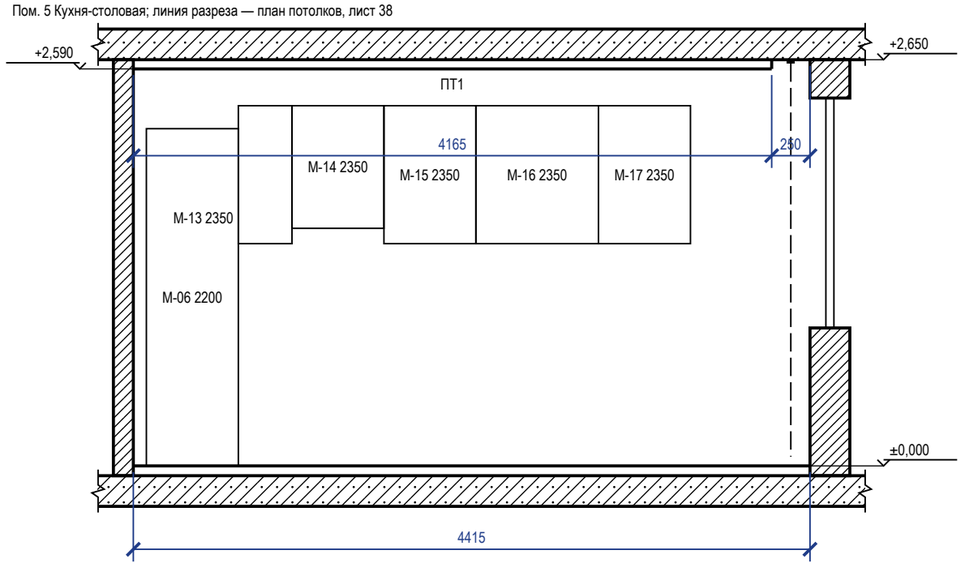


Разрез 2–2 (М 1:40)

Пом. 7 Спальня; линия разреза — план потолков, лист 38

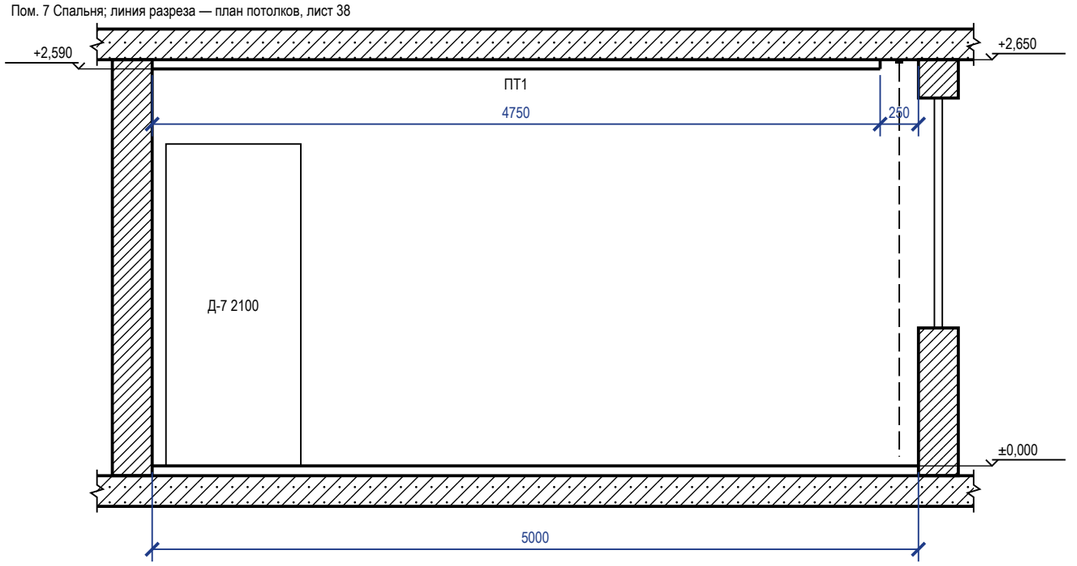

1 Ниша под шторы (М 1:10)

Пом. 5, 7; без подсветки; закладные под карниз — до обшивки

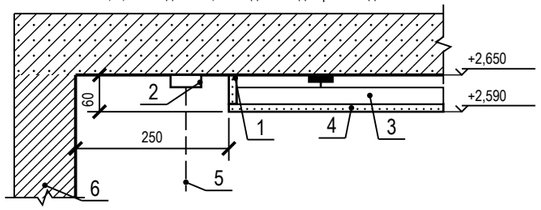

1 — стенка ниши — ГКЛ 12,5
2 — карниз (шина), высота с верхом портьеры 60 мм
3 — ПП 60×27 — каркас короба
4 — низ короба нижнего уровня — ГКЛ 12,5
5 — портьера
6 — стена с окном

Условные обозначения

- плита перекрытия в сечении
- стена в сечении
- потолок ГКЛ в сечении; под линией — марка потолка (план потолков)
- мебель и дверные проёмы за секущей плоскостью; число — марка и верх от чистого пола, мм
- портьера в нише под шторы


Примечания

1. Разрезы — по линиям 1–1, 2–2 на плане потолков (лист 38). Отметки — от ±0,000 чистого пола, м; размеры — мм.
2. Высоты мебели и дверных блоков за секущей плоскостью сверены с низом потолка над ними: верх ниже низа короба и поля.
3. ГКЛ 12,5 мм по каркасу П113. Ниша под шторы — на всю длину стены с окном, карниз на закладной до обшивки (узел 1 — на этом листе).
4. Толщины плит перекрытия и пирога пола показаны условно.
5. Сечения потолков по помещениям М 1:10 (отметки помещения, профили, подвесы, крепёж, изделия) — лист 40.
6. Ведомость объёмов потолков (лист ГКЛ, профиль, подвесы, лента, блоки питания, люки) — на листе 40.

	Лист	№ док.	Подпись	Дата	Проект: Квартира 68 м², элитный модерн			М 1:40; 1:10
Дизайнер	Кырлан А.С.			13.11.26	Разрезы и узлы потолков	Стадия	Лист	Листов
Проверил						П	39	94
Н. контр.								
Утв.								

Сечение 5.1. Ниша под шторы (М 1:10)

Пом. 5 Кухня-столовая, 7 Спальня; без подсветки; закладные под карниз — до обшивки

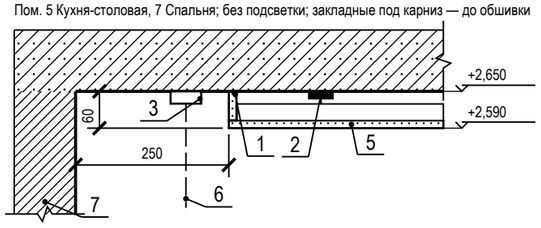

1 — стенка ниши — ГКЛ 12,5

2 — анкер-клин к плите — по одному на подвес; подвес прямой, шаг 1000 мм

3 — карниз (шина), высота с верхом портьеры 60 мм

4 — ПП 60×27 — каркас короба, основные через 1200 мм; соединители одноуровневые, шурупы LN 3,5×9


5 — низ короба нижнего уровня — ГКЛ 12,5; шурупы TN 3,5×25 через 170 мм

6 — портьера

7 — стена с окном

Сечение 5.2. Примыкание потолка к стене (М 1:10)

Пом. 5 Кухня-столовая, 7 Спальня; примыкание — теневой шов

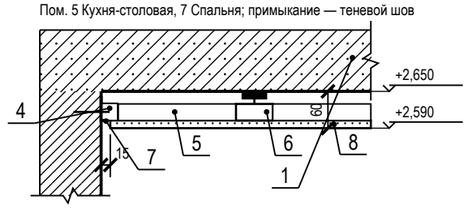

1 — плита перекрытия

2 — анкер-клин к плите — по одному на подвес

3 — подвес прямой, шаг 1000 мм

4 — ПН 28×27 по периметру — дюбель-гвоздь через ≤ 500 мм, не менее 3 на профиль

5 — ПП 60×27 несущий (вид) через 500 мм, в ПН

6 — ПП 60×27 основной (сечение) через 1200 мм; соединители одноуровневые, шурупы LN 3,5×9

7 — теневой профиль: шов 15 мм, зазор 3 мм; стена под шов выровнена

8 — ГКЛ 12,5 по П113; шурупы TN 3,5×25 через 170 мм

Ведомость объёмов потолков


Позиция	Ед.	Кол.	Пом.
Лист ГКЛ 12,5	м²	62,91	1, 4, 5, 6, 7
Лист ГКЛВ 12,5	м²	5,81	2, 3
Борта и карнизы (входят в площади листов выше)	м²	0,69	4, 5, 7
Профиль ПП 60×27	м	194,45	1, 2, 3, 4, 5, 6, 7
Профиль ПН 28×27	м	104,41	1, 2, 3, 4, 5, 6, 7
Подвес прямой	шт.	61	1, 2, 3, 4, 5, 6, 7
Анкер-клин к плите	шт.	61	1, 2, 3, 4, 5, 6, 7
Шуруп TN 3,5×25	шт.	1581	1, 2, 3, 4, 5, 6, 7
Лента армирующая для швов	м	82,46	1, 2, 3, 4, 5, 6, 7
Шпаклёвка для швов	кг	27,49	1, 2, 3, 4, 5, 6, 7
Грунтовка (швы)	л	6,87	1, 2, 3, 4, 5, 6, 7
Лента разделительная по периметру	м	87,03	1, 2, 3, 4, 5, 6, 7
Сплошная шпаклёвка и окраска (площадь развёртки)	м²	68,72	1, 2, 3, 4, 5, 6, 7

Примечания

1. Сечения потолков М 1:10 по помещениям с нишами LED и нишами под шторы: отметки и размеры этого помещения от ±0,000 чистого пола (м, мм). Положение — по плану потолков (лист 38): короб и ниша LED — по линиям ленты, ниша под шторы — у стены с окном; типовые узлы по группам помещений — на листе 39.
2. Крепёж: подвес прямой к плите на анкер-клине — по одному на подвес (Knauf П113); ПН к стенам — дюбель-гвоздь через ≤ 500 мм, не менее 3 на профиль (серия 1.045.9-2.08); лист 12,5 — шурупы TN 3,5×25 через 170 мм (СП 163, табл. 15); профили между собой — соединители одноуровневые, шурупы LN 3,5×9.
3. Изделие карниза, профиля LED и галтели подписано артикулом из данных; где артикул не выбран, сечение дано по габаритам из данных (ширина и глубина ниши, щель под свет), изделие подбирается по ним.
4. Ведомость объёмов — по геометрии плана потолков: Лист ГКЛ 12,5 — плоскости уровней + борта (без арочных участков); Лист ГКЛВ 12,5 — плоскости уровней + борта; Борта и карнизы — длина перепада × перепад; Профиль ПП 60×27 — S × (1/шаг несущ. + 1/шаг осн.) + стойки бортов; Профиль ПН 28×27 — периметр стен + 2 × перепады + карнизы; Подвес прямой — по раскладке: S уровня / (шаг осн. × шаг подвесов), пояс уже шага — ряд вдоль пояса, фигура — по контуру; шаг подвесов — не больше табл. 14 СП 163; Анкер-клин к плите — по одному на подвес (Knauf П113); Шуруп TN 3,5×25 — 23 шт./м² (Knauf П113, табл. 2 альбома П 11); Лента армирующая для швов — 1,2 м/м² листа (Knauf); Шпаклёвка для швов — 0,4 кг/м² листа, только швы (Knauf); Грунтовка (швы) — 0,1 л/м² листа, только швы (Knauf); Лента разделительная по периметру — периметр стен под потолком ГКЛ; Сплошная шпаклёвка и окраска (площадь развёртки) — плоскости + борта; расход — по паспорту материала (норма расхода на сплошной слой не подтверждена); без запаса на подрезку (при закупке листа: ×1,075 при S > 20 м², ×1,175 — 10–20 м², ×1,275 — < 10 м²).

	Лист	№ док.	Подпись	Дата	Проект: Квартира 68 м², элитный модерн			М 1:10
Дизайнер	Кырлан А.С.			13.11.26	Сечения потолков М 1:10	Стадия	Лист	Листов
Проверил						П	40	94
Н. контр.								
Утв.								

выпуск 13.11.2026 № c38d47cb31 · стр. 40 из 94

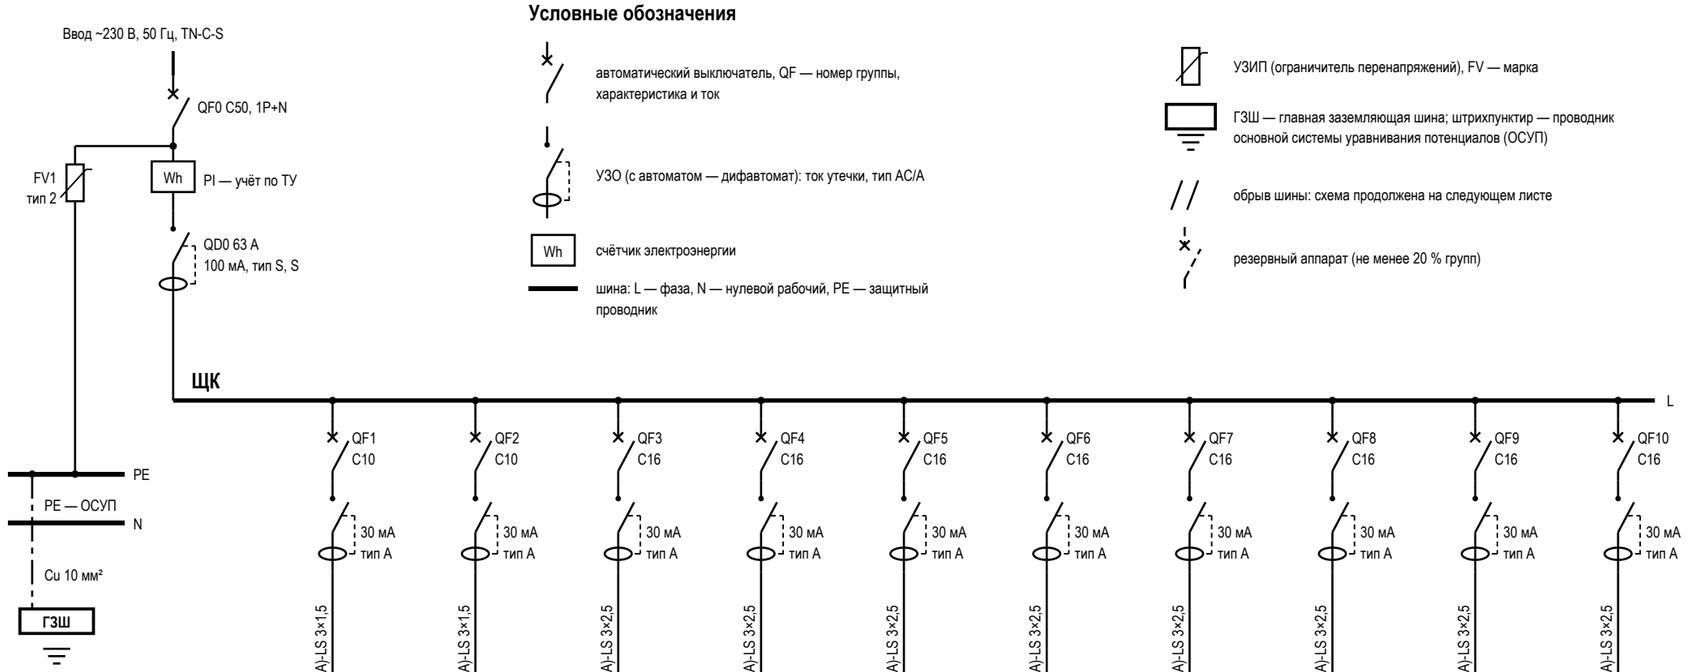

Условные обозначения

- автоматический выключатель, QF — номер группы, характеристика и ток
- УЗО (с автоматом — дифавтомат): ток утечки, тип AC/A
- Wh — счётчик электроэнергии
- шина: L — фаза, N — нулевой рабочий, PE — защитный проводник
- УЗИП (ограничитель перенапряжений), FV — марка
- ГЗШ — главная заземляющая шина; штрихпунктир — проводник основной системы уравнивания потенциалов (ОСУП)
- обрыв шины: схема продолжена на следующем листе
- резервный аппарат (не менее 20 % групп)

Данные щитка

Показатель	Значение
Номер щитка	ЩК
Тип	ЩРВ-П-72, IP41
Уст. мощность, кВт	33,1
Разреш. мощность, кВт	10
Расчётная, кВт	10,8
Расчётная > разрешённой	10,8 > 10 кВт: превышение 0,8 кВт
Автоматы 1п: занят. / рез.	20 / 4
Модулей: всего / занято	72 / 46
Ток на вводе, А	50
Вводной аппарат	QF0 C50, 1P+N
УЗИП	FV1, тип 2, ЩК, после счётчика
ГЗШ, проводник ОСУП	Cu 10 мм²
Листов схемы	2 (группы по листам)

Таблица групп щита ЩК и кабельный журнал

№	Назначение	Помещения	Автомат	УЗО / дифавтомат	Кабель	Длина, м	Р, кВт	Точек
1	освещение: кабинет, прихожая, кухня-столовая, гостиная, спальня	1, 4, 5, 6, 7	C10	30 мА, тип A	ВВГнг(A)-LS 3×1,5	85	0,6	52
2	освещение и вентиляторы санузлов	2, 3, 4	C10	30 мА, тип A	ВВГнг(A)-LS 3×1,5	36	0,2	11
3	розетки: кабинет	1	C16	30 мА, тип A	ВВГнг(A)-LS 3×2,5	41	1,5	9
4	розетки: кухня-столовая	5	C16	30 мА, тип A	ВВГнг(A)-LS 3×2,5	41	1,5	1
5	розетки: гостиная	6	C16	30 мА, тип A	ВВГнг(A)-LS 3×2,5	41	2	10
6	розетки: спальня	7	C16	30 мА, тип A	ВВГнг(A)-LS 3×2,5	41	1,5	11
7	розетки: прихожая	4	C16	30 мА, тип A	ВВГнг(A)-LS 3×2,5	30	1	1
8	розетки фартука кухни (мелкая техника)	5	C16	30 мА, тип A	ВВГнг(A)-LS 3×2,5	18	2,5	6
9	розетки: чайник и кофемашина (отдельная линия)	5	C16	30 мА, тип A	ВВГнг(A)-LS 3×2,5	18	2,2	1
10	холодильник	5	C16	30 мА, тип A	ВВГнг(A)-LS 3×2,5	18	0,4	1

Примечания

1. Схема однолинейная: одна линия — фаза, N и PE группы; аппараты — в отключённом положении (ГОСТ 2.702, ГОСТ 2.755). Номера групп — как у точек на планах (гр.). За отметку 0,000 принят уровень чистого пола; высота щита — по плану розеток.
2. Розеточные и мокрые линии — через УЗО или дифавтомат с током утечки не более 30 мА (ПУЭ 7.1.79); в санузле выполнить ДСУП (ПУЭ 7.1.87–7.1.88).
3. УЗО тип A — для линий с электроникой, стиральной и посудомоечной машиной, LED-драйверами; тип AC — только для чисто активной нагрузки.
4. Кабель — медный, исполнение нг(A)-LS (ГОСТ 31565-2012); скрытая прокладка только горизонтально и вертикально, фактические трассы зафиксировать исполнительной схемой до закрытия отделкой.
5. Номинал автомата — не выше допустимого тока кабеля: 1,5 мм² — до 10 А, 2,5 мм² — до 16 А. Резерв щита — не менее 20 % модулей.
6. Расчёт нагрузок, токов КЗ, селективности и сечений — по проекту ЭОМ организации с допуском СРО; лист задаёт состав, расположение и группы.
7. УЗИП FV1 — после вводного автомата, проводник к шине PE — кратчайший, без петель. Шина PE щита соединяется с ГЗШ проводником ОСУП; к ГЗШ присоединяются трубы водопровода и отопления на вводе в квартиру (ПУЭ 7.1.87). Шины N и PE — раздельные, после разделения PEN не объединяются.
8. До подключения нагрузки — приёмо-сдаточные испытания с протоколом: сопротивление изоляции линий не менее 0,5 МОм, срабатывание УЗО по току и времени, непрерывность защитных проводников PE (ПУЭ, гл. 1.8).

	Лист	№ док.	Подпись	Дата	Проект: Квартира 68 м², элитный модерн			
Дизайнер	Кырлан А.С.			13.11.26	Однолинейная схема щита	Стадия	Лист	Листов
Проверил						П	41	94
Н. контр.								
Утв.								

Продолжение однолинейной схемы щита ЩК, начало — лист 41

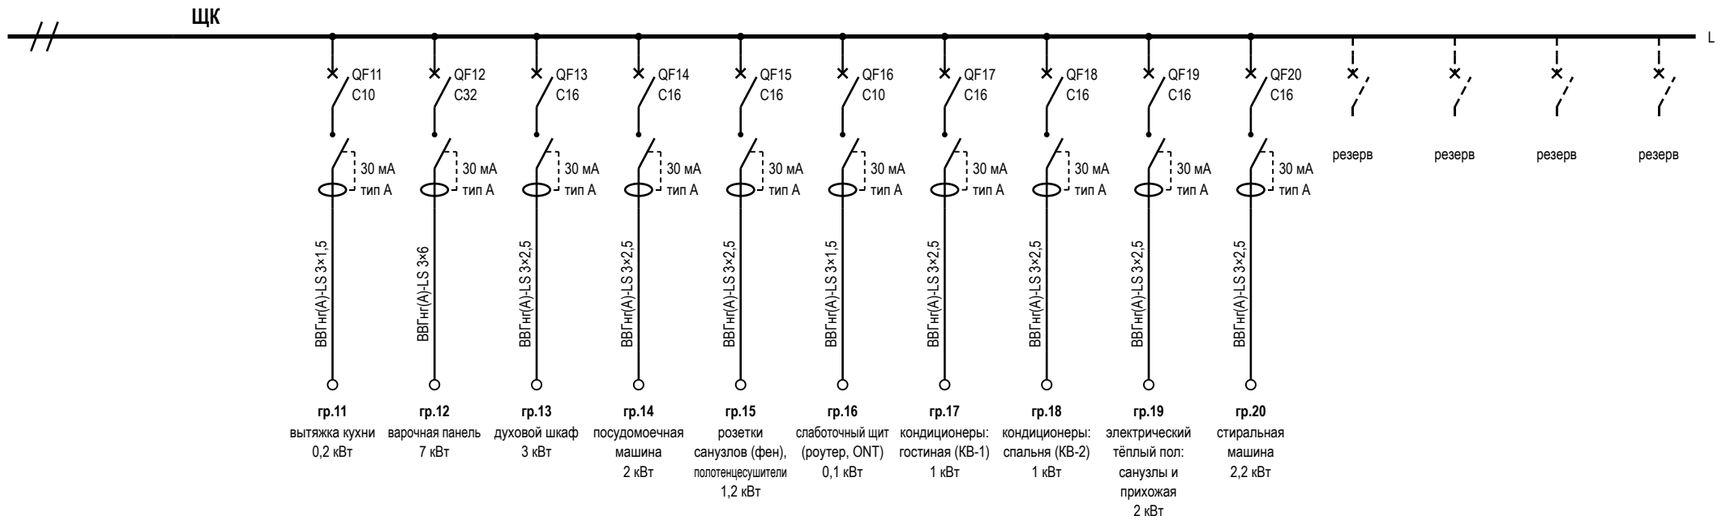


Таблица групп щита ЩК и кабельный журнал (продолжение)

№	Назначение	Помещения	Автомат	УЗО / дифавтомат	Кабель	Длина, м	Р, кВт	Точек
11	вытяжка кухни	5	C10	30 мА, тип A	ВВГнг(A)-LS 3×1,5	18	0,2	1
12	варочная панель	5	C32	30 мА, тип A	ВВГнг(A)-LS 3×6	18	7	1
13	духовой шкаф	5	C16	30 мА, тип A	ВВГнг(A)-LS 3×2,5	18	3	1
14	посудомоечная машина	5	C16	30 мА, тип A	ВВГнг(A)-LS 3×2,5	18	2	1
15	розетки санузлов (фен), полотенцесушители	2, 3	C16	30 мА, тип A	ВВГнг(A)-LS 3×2,5	27	1,2	2
16	слаботочный щит (роутер, ONT)	4	C10	30 мА, тип A	ВВГнг(A)-LS 3×1,5	6	0,1	6
17	кондиционеры: гостиная (КВ-1)	6	C16	30 мА, тип A	ВВГнг(A)-LS 3×2,5	41	1	1
18	кондиционеры: спальня (КВ-2)	7	C16	30 мА, тип A	ВВГнг(A)-LS 3×2,5	41	1	1
19	электрический тёплый пол: санузлы и прихожая	3, 4	C16	30 мА, тип A	ВВГнг(A)-LS 3×2,5	18,8	2	2
20	стиральная машина	3	C16	30 мА, тип A	ВВГнг(A)-LS 3×2,5	15	2,2	1
	Итого по сечениям ВВГнг(A)-LS (все группы щита), м: 3×1,5 — 145; 3×2,5 — 426,8; 3×6 — 18					589,8		

Примечания

1. Лист — продолжение однолинейной схемы щита ЩК: начало, данные щитка и условные обозначения — лист 41. Ввод, учёт, вводной аппарат, УЗИП, шины N и PE и ГЗШ показаны там же; шина L листа — та же шина щита.
2. Схема однолинейная: одна линия — фаза, N и PE группы; аппараты — в отключённом положении (ГОСТ 2.702, ГОСТ 2.755). Номера групп — как у точек на планах (гр.). За отметку 0,000 принят уровень чистого пола; высота щита — по плану розеток.
3. Розеточные и мокрые линии — через УЗО или дифавтомат с током утечки не более 30 мА (ПУЭ 7.1.79); в санузле выполнить ДСУП (ПУЭ 7.1.87–7.1.88).
4. УЗО тип A — для линий с электроникой, стиральной и посудомоечной машиной, LED-драйверами; тип AC — только для чисто активной нагрузки.
5. Кабель — медный, исполнение нг(A)-LS (ГОСТ 31565-2012); скрытая прокладка только горизонтально и вертикально, фактические трассы зафиксировать исполнительной схемой до закрытия отделкой.
6. Номинал автомата — не выше допустимого тока кабеля: 1,5 мм² — до 10 А, 2,5 мм² — до 16 А. Резерв щита — не менее 20 % модулей.
7. Расчёт нагрузок, токов КЗ, селективности и сечений — по проекту ЭОМ организации с допуском СРО; лист задаёт состав, расположение и группы.
8. До подключения нагрузки — приёмо-сдаточные испытания с протоколом: сопротивление изоляции линий не менее 0,5 МОм, срабатывание УЗО по току и времени, непрерывность защитных проводников PE (ПУЭ, гл. 1.8).

	Лист	№ док.	Подпись	Дата	Проект: Квартира 68 м², элитный модерн			
Дизайнер	Кырлан А.С.			13.11.26	Однолинейная схема щита (продолжение)	Стадия	Лист	Листов
Проверил						П	42	94
Н. контр.								
Утв.								

Группы щита ЩК (1)

№	Назначение	Руст, кВт	Кс	Ррасч, кВт	Iрасч, А	Автомат	Кабель
1	освещение: кабинет, прихожая, кухня-столовая, гостиная, спальня	0,6	0,6	0,36	1,6	C10	3×1,5
2	освещение и вентиляторы санузлов	0,2	0,6	0,12	0,5	C10	3×1,5
3	розетки: кабинет	1,5	0,4	0,6	2,7	C16	3×2,5
4	розетки: кухня-столовая	1,5	0,4	0,6	2,7	C16	3×2,5
5	розетки: гостиная	2	0,4	0,8	3,7	C16	3×2,5
6	розетки: спальня	1,5	0,4	0,6	2,7	C16	3×2,5
7	розетки: прихожая	1	0,4	0,4	1,8	C16	3×2,5
8	розетки фартука кухни (мелкая техника)	2,5	0,4	1	4,6	C16	3×2,5
9	розетки: чайник и кофемашина (отдельная линия)	2,2	0,4	0,88	4	C16	3×2,5
10	холодильник	0,4	0,4	0,16	0,7	C16	3×2,5

Группы щита ЩК (2)

№	Назначение	Руст, кВт	Кс	Ррасч, кВт	Iрасч, А	Автомат	Кабель
11	вытяжка кухни	0,2	0,4	0,08	0,4	C10	3×1,5
12	варочная панель	7	0,6	4,2	19,2	C32	3×6
13	духовой шкаф	3	0,6	1,8	8,2	C16	3×2,5
14	посудомоечная машина	2	0,7	1,4	6,4	C16	3×2,5
15	розетки санузлов (фен), полотенцесушители	1,2	0,7	0,84	3,8	C16	3×2,5
16	слаботочный щит (роутер, ONT)	0,1	0,4	0,04	0,2	C10	3×1,5
17	кондиционеры: гостиная (КВ-1)	1	0,8	0,8	3,7	C16	3×2,5
18	кондиционеры: спальня (КВ-2)	1	0,8	0,8	3,7	C16	3×2,5
19	электрический тёплый пол: санузлы и прихожая	2	1	2	9,2	C16	3×2,5
20	стиральная машина	2,2	0,7	1,54	7	C16	3×2,5

Итог по квартире

Показатель	Значение
Установленная мощность Σ Руст	33,1 кВт
Σ Руст × Кс по группам	19,02 кВт
Коэффициент одновременности	0,7
Расчётная мощность квартиры Ррасч	13,3 кВт
Расчётный ток Iрасч (230 В, cosφ 0,95)	61 А
Разрешённая мощность	10 кВт
Запас до разрешённой	-33,1 % — меньше 10 %
Вводной аппарат	C50, 1P+N


Примечания

1. Руст — установленная мощность группы по данным щита (приборы — по паспорту, розетки общего назначения — оценка 0,1 кВт на гнездо). Кс — коэффициенты спроса: освещение 0,6; розетки 0,4; варочная и духовой 0,6; кондиционеры 0,8; тёплый пол 1,0; прочие 0,7; одновременность 0,7.
2. Коэффициенты — ориентир исполнителя, не табличные значения нормы; расчёт нагрузки подтверждает инженер ЭОМ (СП 256.1325800.2016). Под разрешённую мощность они не подгоняются.
3. Вывод: расчётная 13,3 кВт больше разрешённой 10 кВт на 3,3 кВт. Это вопрос заказчику (реестр K-N): запросить увеличение мощности у сетевой организации либо принять приоритетное отключение нагрузок (тёплый пол, кондиционеры, вторая машина) при работе плиты.
4. Розеточные и мокрые линии — через УЗО или дифавтомат с током утечки не более 30 мА (ПУЭ 7.1.79); в санузле выполнить ДСУП (ПУЭ 7.1.87–7.1.88).

	Лист	№ док.	Подпись	Дата	Проект: Квартира 68 м², элитный модерн			
Дизайнер	Кырлан А.С.			13.11.26	Таблица нагрузок щита	Стадия	Лист	Листов
Проверил						П	43	94
Н. контр.								
Утв.								

выпуск 13.11.2026 № c38d47cb31 · стр. 43 из 94

План принципиальных трасс (М 1:75)

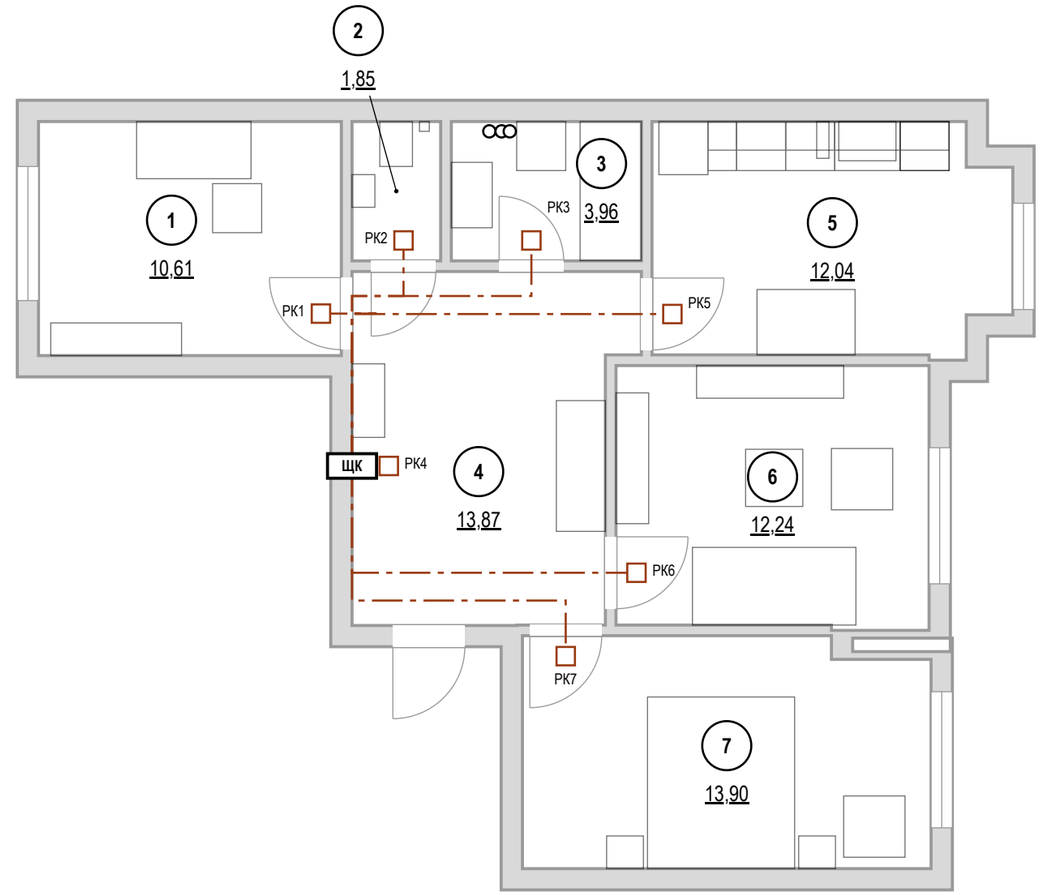

Кабель по группам ВВГнг(А)-LS, м

Гр.	мм²	Трасса	Данные
1	3×1,5	135,1	85
2	3×1,5	31,7	36
3	3×2,5	32	41
4	3×2,5	17,5	41
5	3×2,5	35,6	41
6	3×2,5	39,4	41
7	3×2,5	4,7	30
8	3×2,5	28,5	18
9	3×2,5	16	18
10	3×2,5	10,8	18

Гр.	мм²	Трасса	Данные
11	3×1,5	11,7	18
12	3×6	14,4	18
13	3×2,5	14,4	18
14	3×2,5	16,5	18
15	3×2,5	18,6	27
16	3×1,5	22,3	6
17	3×2,5	10,6	41
18	3×2,5	8,5	41
19	3×2,5	18,8	
20	3×2,5	14,4	15
Σ		**501,5**	**571**

Экспликация помещений

№	Помещение	Площадь, м²
1	Кабинет	10,61
2	Санузел	1,85
3	Ванная	3,96
4	Прихожая	13,87
5	Кухня-столовая	12,04
6	Гостиная	12,24
7	Спальня	13,90
	Итого (общая площадь)	68,47

Объёмы прокладки

Работа, материал	Ед.	Кол.
Гофротруба Ø20 в потолочном пространстве	м	218,4
Кабель-канал плинтуса для силовых линий	м	114,5
Короб или накладной канал для вертикальных спусков и подъёмов	м	86,9
Коробка распределительная (РК) над дверью помещения	шт	7
Слаботочка: кабель домофона	м	3,1
Слаботочка: Кабель коаксиальный RG-6 (75 Ом) к розеткам ТВ	м	14,1
Слаботочка: Кабель U/UTP кат. 5е (LAN, Wi-Fi и камеры по PoE)	м	27,4
Слаботочка: U/UTP кат. 6 (LAN, Wi-Fi, камеры)	м	2,7
Слаботочка: гофротруба Ø20 отдельно от силовых	м	42,6

Штробы — только после заключения

Работа	Ед.	Кол.
Вертикальные штробы 20×20 мм от потолка до каждой настенной точки (в маршрут без штроб не входят)	м	119,2

Условные обозначения


- **ЩК** — щит квартирный
- РК — распределительная коробка над дверью помещения
- магистраль от щита к РК: потолочное пространство, гофра
- мебель и сантехприборы — подложка

Примечания

1. За отметку 0,000 принят уровень чистого пола. Высоты Н — от чистого пола до оси изделия; привязки — от чистовой грани стены до оси механизма (у рамки на несколько постов — до оси рамки).
2. Розеточные и мокрые линии — через УЗО или дифавтомат с током утечки не более 30 мА (ПУЭ 7.1.79); в санузле выполнить ДСУП (ПУЭ 7.1.87–7.1.88).
3. Кабель — медный, исполнение нг(А)-LS (ГОСТ 31565-2012); скрытая прокладка только горизонтально и вертикально, фактические трассы зафиксировать исполнительной схемой до закрытия отделкой.
4. Расчёт нагрузок, токов КЗ, селективности и сечений — по проекту ЭОМ организации с допуском СРО; лист задаёт состав, расположение и группы.
5. Длины — по плану: от щита вверх в потолочное пространство, по дверям и коридору без захода в мокрые помещения к распределительной коробке над дверью, далее к точкам; вертикали считаются вниз и обратно (у последней точки цепочки — в один конец); запас 10 %. Трассы принципиальные: фактическую зафиксировать исполнительной схемой до закрытия отделкой.
6. Несущие стены не определены: штробы в стенах не выполнять. Маршрут проложен без штроб: горизонтали — за потолком в гофре (218,4 м) и в кабель-канале плинтуса (114,5 м), вертикали — в коробе или накладном канале (153 м кабеля). Точек: за потолком — 47, спуск из потолка — 13, по плинтусу — 26, плинтус и подъём — 34.
7. Вариант со штробами — работа после технического заключения: 119,2 м вертикальных штроб от потолка до каждой настенной точки; условие — только после технического заключения: стена не несущая (или вертикальная штроба в несущей согласована конструктором), глубина и ширина 20–25 мм, не в зонах 0–2 ванной. Без заключения и согласования конструктора в смету и в график эта работа не входит.
8. В данных проекта (журнал щита) длины кабеля внесены оценкой (571 м), по трассам из геометрии — 502 м (-12 %): к закупке и в смету принимать длины по трассам, а оценку в данных проекта заменить.
9. Слаботочные сети: кабели и точки считаются по лучам от ЩС (лист слаботочных сетей): 47 м, портов патч-панели и коммутатора не менее 3; из точек 1 предложения листа слаботочки, не подтверждённые заказчиком. Изделия — в ведомости изделий.

	Лист	№ док.	Подпись	Дата	Проект: Квартира 68 м², элитный модерн	М 1:75		
Дизайнер	Кырлан А.С.			13.11.26	План принципиальных трасс	Стадия	Лист	Листов
Проверил						П	44	94
Н. контр.								
Утв.								

План розеток (М 1:50)

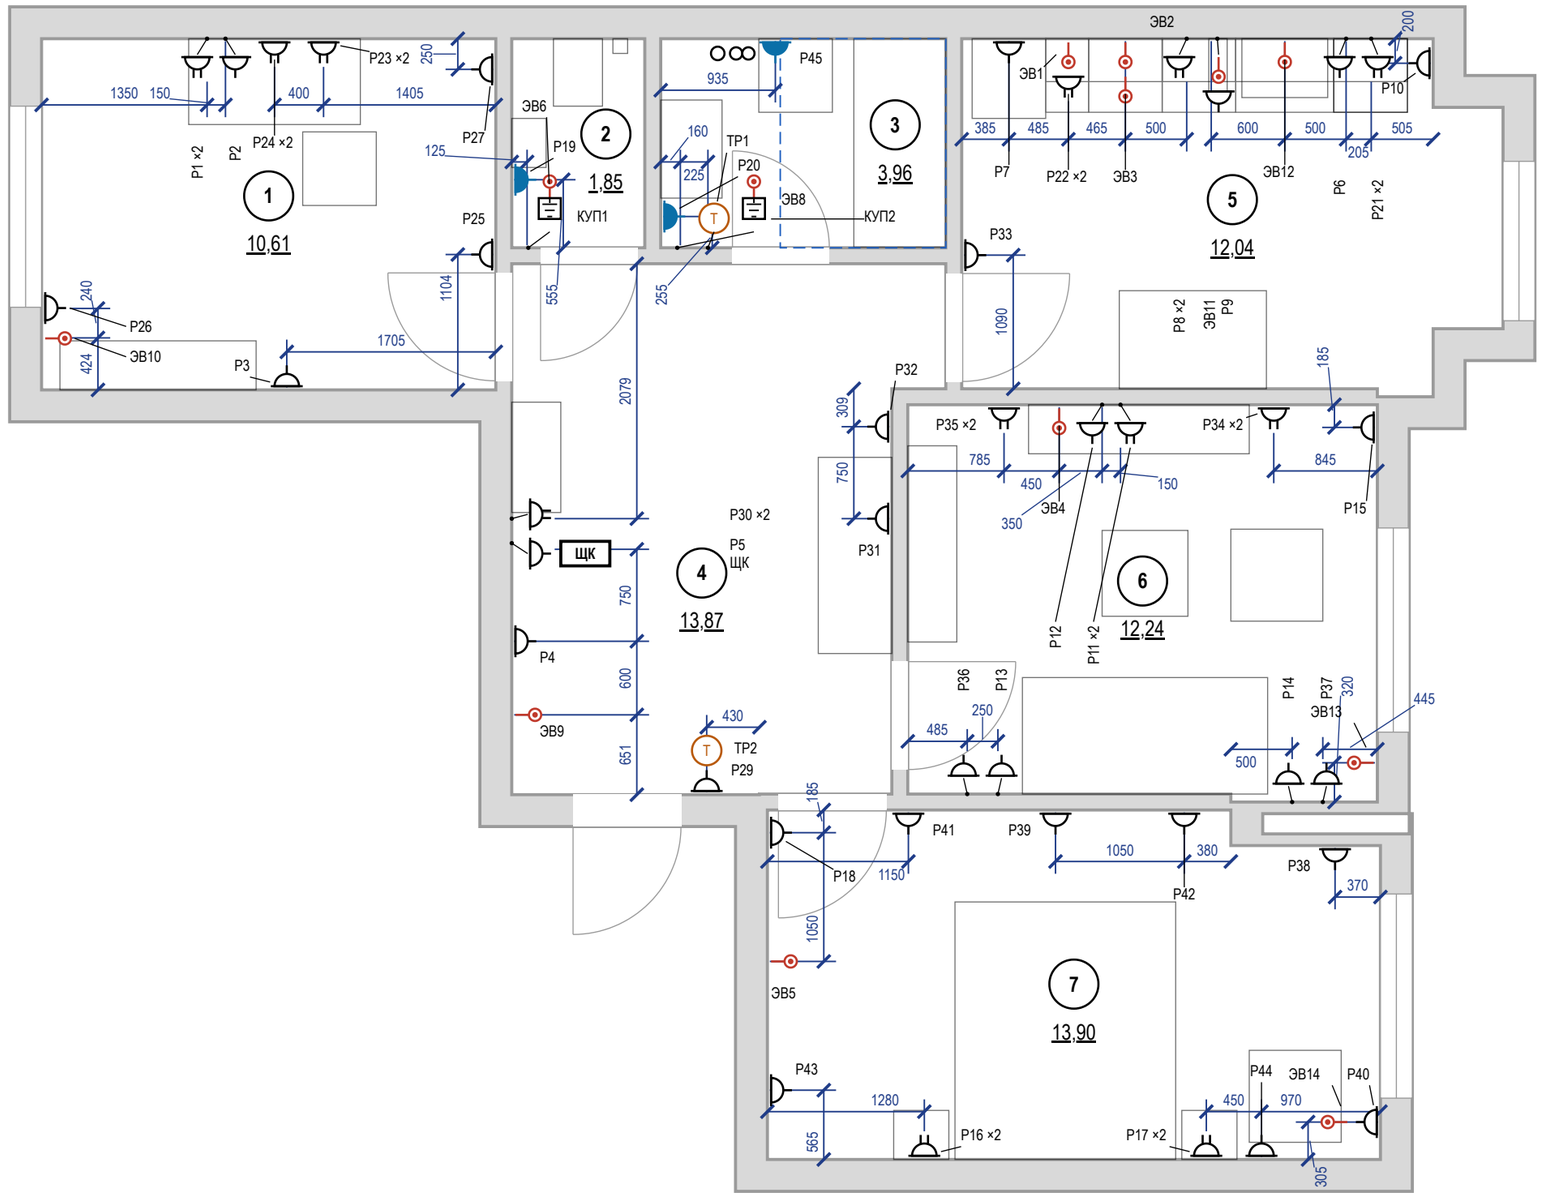

Условные обозначения

Знак	Тип изделия	H, мм	Кол., шт
	Розетка с заземлением	300	24
	То же	у знака	5
	Блок розеток с заземлением, рамка 2 поста	у знака	12
	Розетка с заземлением IP44	1100	3
	Вывод кабеля к прибору	у знака	13
	КУП (уравнивание потенциалов)	300	2
T	Терморегулятор тёплого пола	1000	2
ЩК	Щит квартирный	1700	1

розетка с заземляющим контактом; у знака — марка и ×N — число постов в рамке; группа щита, высота оси и назначение — в ведомости точек

знак разведён для читаемости: точка на стене — у выноски, привязка — до неё

граница зоны 2 ванной (600 мм от ванны/поддона)

мебель и сантехприборы — подложка

стояк: К1 — канализация, В1 — ХВС, Т3 — ГВС

1 номер помещения, площадь м²

Итого розеток (механизмов) — 56 шт; рамок — 44 шт: на 1 пост — 32, на 2 поста — 12.


Примечания

1. За отметку 0,000 принят уровень чистого пола. Высоты H — от чистого пола до оси изделия; привязки — от чистовой грани стены до оси механизма (у рамки на несколько постов — до оси рамки).
2. Высоты H и группы щита — в ведомости электроточек: розетки — 300 мм от чистого пола до оси механизма, если в ведомости не указано иное; выводы кабеля — по паспорту прибора.
3. Розетки в санузле — только вне зон 0–2 (ПУЭ 7.1.48, ГОСТ Р 50571.7.701-2024), IP44, через УЗО 30 мА.
4. Розеточные и мокрые линии — через УЗО или дифавтомат с током утечки не более 30 мА (ПУЭ 7.1.79); в санузле выполнить ДСУП (ПУЭ 7.1.87–7.1.88).
5. Кабель — медный, исполнение нг(А)-LS (ГОСТ 31565-2012); скрытая прокладка только горизонтально и вертикально, фактические трассы зафиксировать исполнительной схемой до закрытия отделкой.
6. Расчёт нагрузок, токов КЗ, селективности и сечений — по проекту ЭОМ организации с допуском СРО; лист задаёт состав, расположение и группы.
7. Выводы кухонной техники — после утверждения проекта кухни (ориентировочно); привязки выводов даны от осей модулей гарнитура и пересматриваются вместе с проектом кухни.

	Лист	№ док.	Подпись	Дата	Проект: Квартира 68 м², элитный модерн			М 1:50
Дизайнер	Кырлан А.С.			13.11.26	План розеток и электровыводов	Стадия	Лист	Листов
Проверил						П	45	94
Н. контр.								
Утв.								

выпуск 13.11.2026 № c38d47cb31 · стр. 45 из 94

План слаботочных сетей (М 1:50)

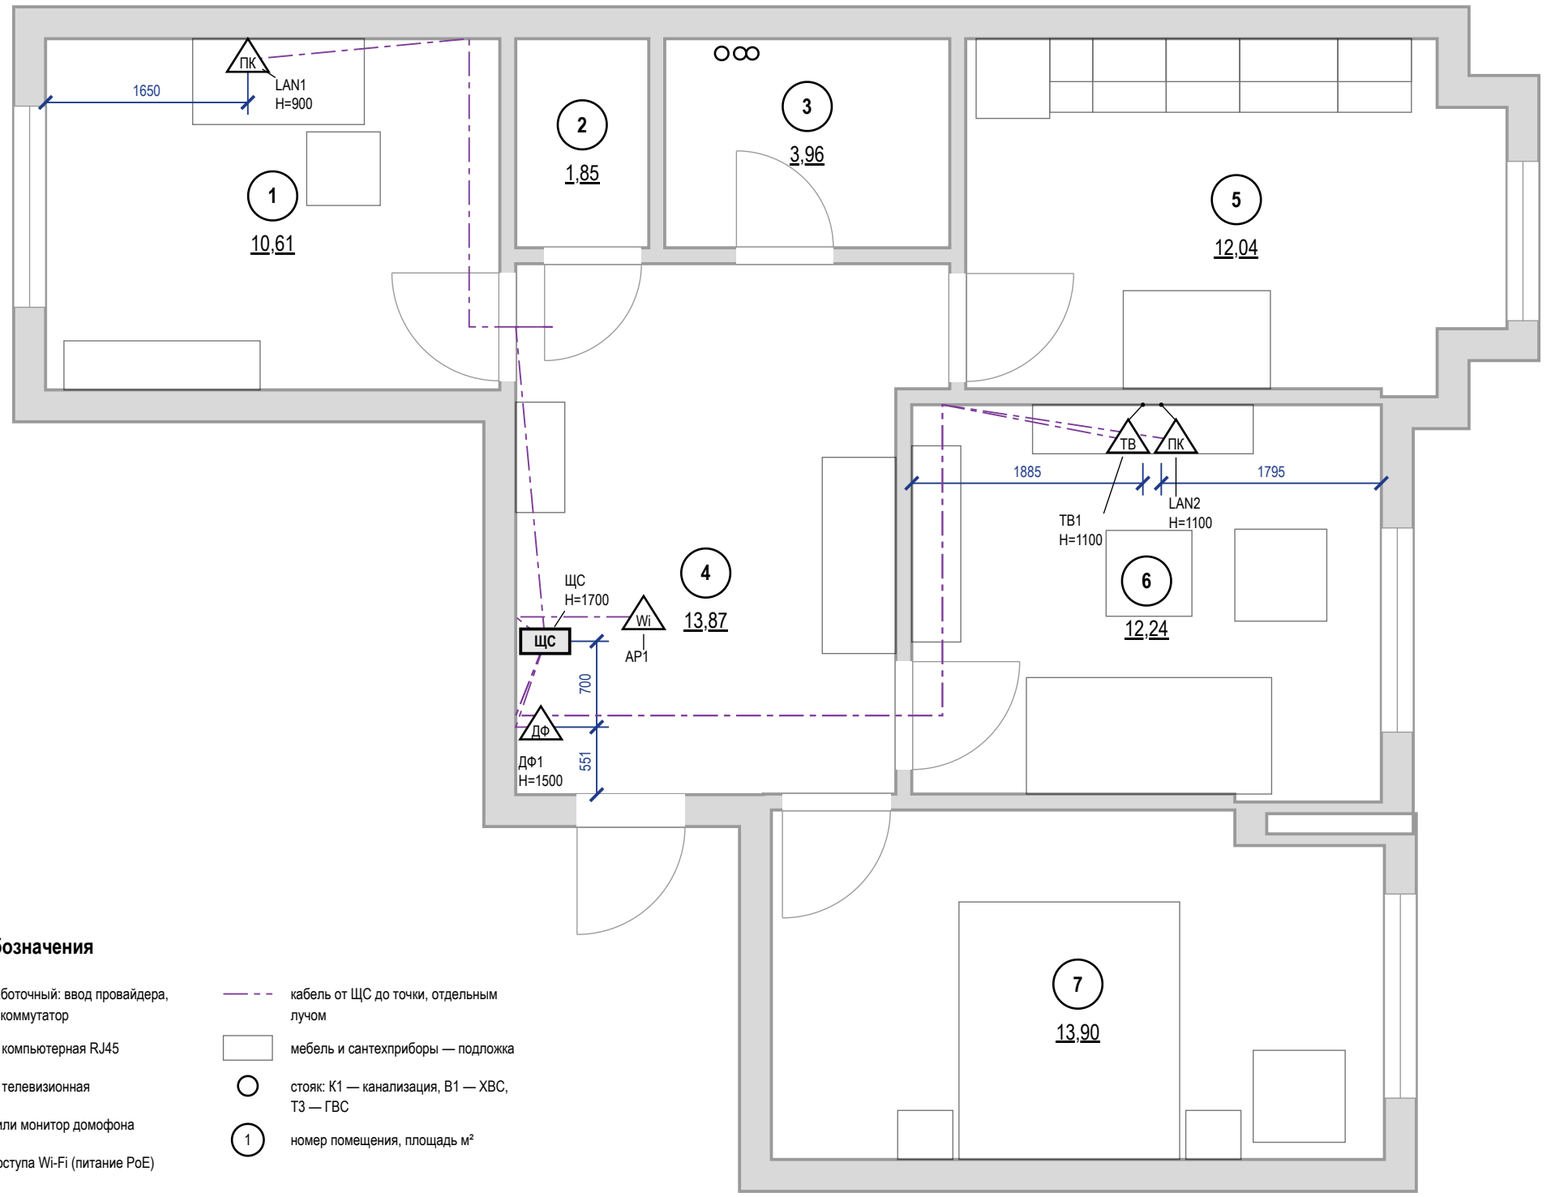

Условные обозначения

ЩС	щит слаботочный: ввод провайдера, роутер, коммутатор
ПК	розетка компьютерная RJ45
ТВ	розетка телевизионная
ДФ	трубка или монитор домофона
Wi	точка доступа Wi-Fi (питание PoE)
— — —	кабель от ЩС до точки, отдельным лучом
▭	мебель и сантехприборы — подложка
○	стояк: К1 — канализация, В1 — ХВС, Т3 — ГВС
1	номер помещения, площадь м²


Примечания

1. За отметку 0,000 принят уровень чистого пола. Высоты Н — от чистого пола до оси изделия; привязки — от чистовой грани стены до оси механизма (у рамки на несколько постов — до оси рамки).
2. Высота установки, не указанная на плане: розетки LAN и ТВ — 300 мм от чистого пола.
3. Слаботочные кабели — отдельно от силовых: в своей трубе или лотке, при параллельной прокладке не ближе 100 мм к силовым, пересечения под прямым углом; каждую точку — отдельным кабелем от ЩС без скруток.
4. Трассы на листе — принципиальные; фактические зафиксировать исполнительной схемой до закрытия отделкой. Силовые линии, УЗО 30 мА, ДСУП, кабель нг(А)-LS — по листам розеток и щита.
5. Проект силовой части и расчёт токов КЗ — по проекту ЭОМ; слаботочная часть согласуется с провайдером и управляющей компанией (домофон, коллективное ТВ).

	Лист	№ док.	Подпись	Дата	Проект: Квартира 68 м², элитный модерн			М 1:50
Дизайнер	Кырлан А.С.			13.11.26	План слаботочных сетей	Стадия	Лист	Листов
Проверил						П	46	94
Н. контр.								
Утв.								

выпуск 13.11.2026 № c38d47cb31 · стр. 46 из 94

План освещения (М 1:50)

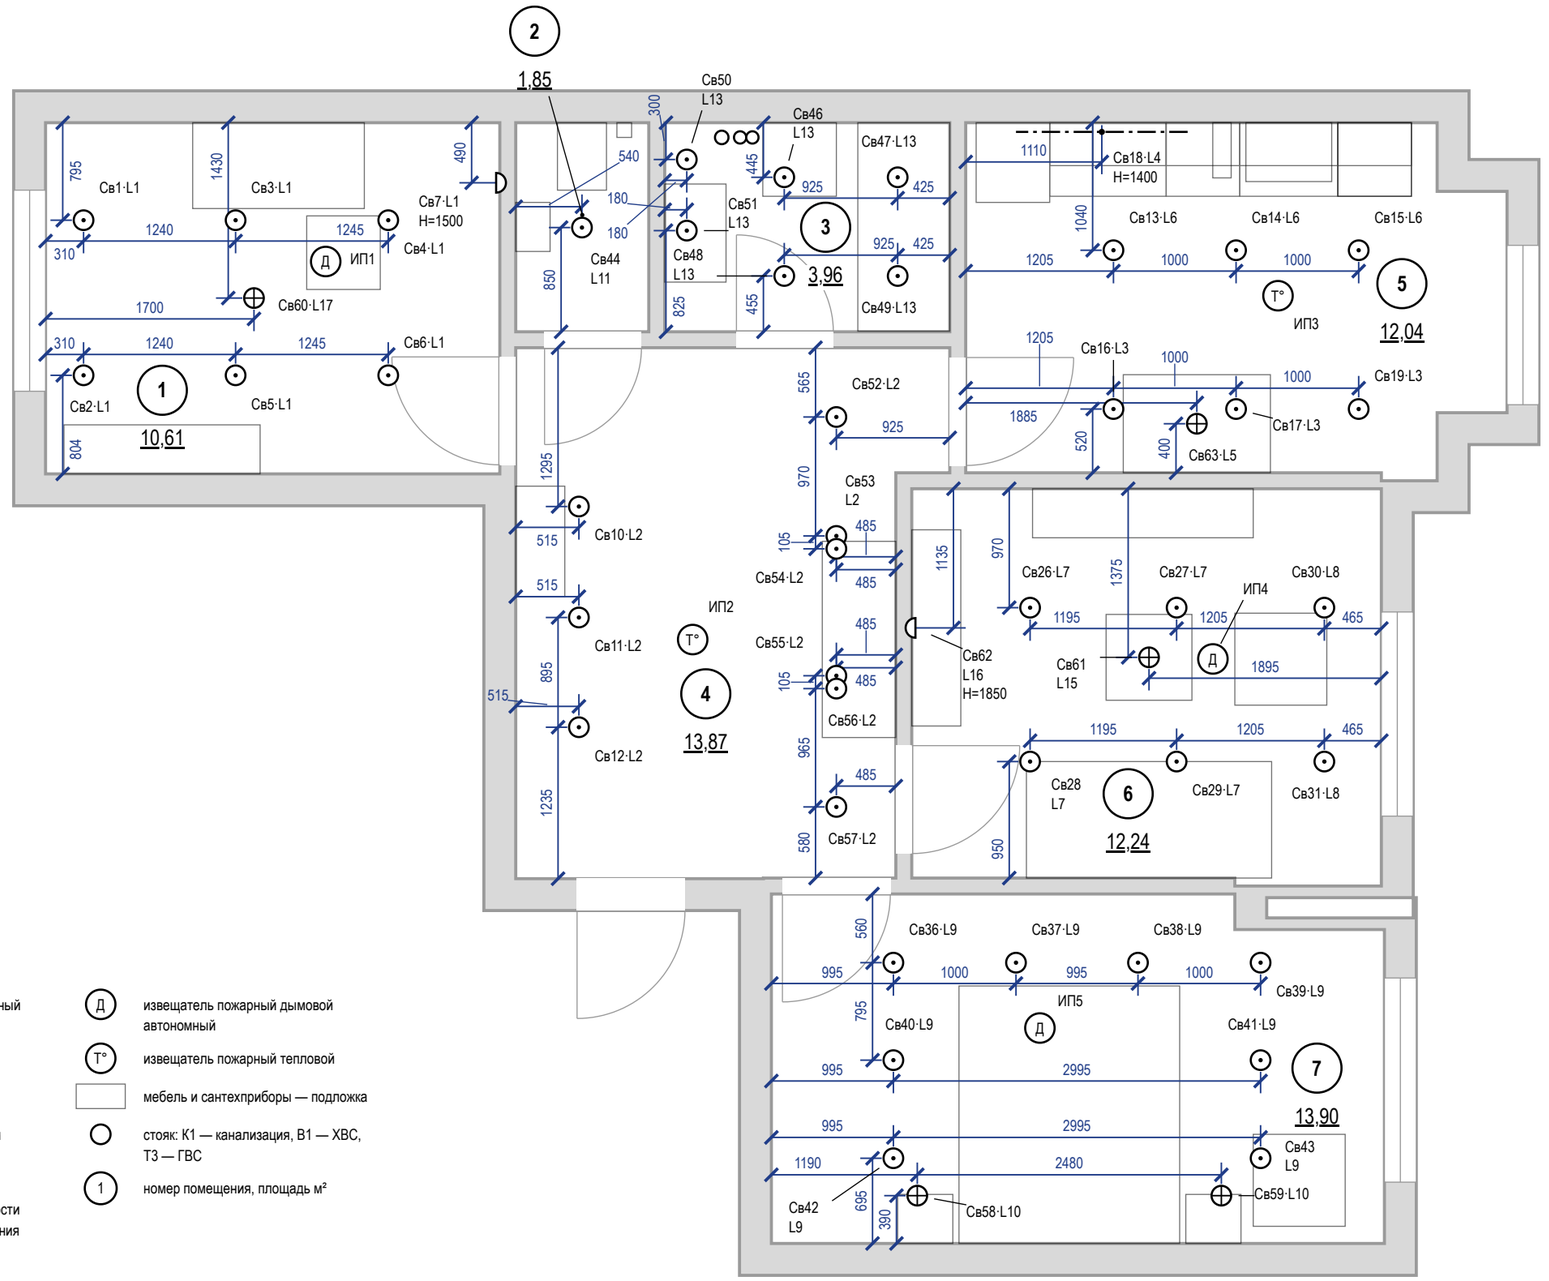

Условные обозначения

- светильник встраиваемый точечный
- светильник подвесной
- светильник настенный (бра), H высота оси
- линейный светильник настенный (подсветка столешницы), точка вывод питания
- Св1·L1 — марка светильника (как в ведомости и на развёртках) · группа включения L (лист 49)
- Д — извещатель пожарный дымовой автономный
- Т° — извещатель пожарный тепловой
- мебель и сантехприборы — подложка
- стояк: К1 — канализация, В1 — ХВС, Т3 — ГВС
- 1 — номер помещения, площадь м²

Примечания

1. За отметку 0,000 принят уровень чистого пола. Высоты H — от чистого пола до оси изделия; привязки — от чистовой грани стены до оси механизма (у рамки на несколько постов — до оси рамки).
2. Высота установки, не указанная на плане: светильники — на потолке; настенные — по отметке H у знака. Привязки — до оси светильника от чистовой грани стены, по рядам.
3. Во влажных помещениях — светильники не ниже IP44; в зонах 0–2 ванной — по ГОСТ Р 50571.7.701-2024 (зона 1 — IPX5).
4. Розеточные и мокрые линии — через УЗО или дифавтомат с током утечки не более 30 мА (ПУЭ 7.1.79); в санузле выполнить ДСУП (ПУЭ 7.1.87–7.1.88).
5. Кабель — медный, исполнение нг(A)-LS (ГОСТ 31565-2012); скрытая прокладка только горизонтально и вертикально, фактические трассы зафиксировать исполнительной схемой до закрытия отделкой.
6. Расчёт нагрузок, токов КЗ, селективности и сечений — по проекту ЭОМ организации с допуском СРО; лист задаёт состав, расположение и группы.
7. Ведомость светильников (тип, количество, мощность, поток, Tц, Ra) — лист 48.

	Лист	№ док.	Подпись	Дата	Проект: Квартира 68 м², элитный модерн	М 1:50		
Дизайнер	Кырлан А.С.			13.11.26				
Проверил					План освещения	Стадия	Лист	Листов
Н. контр.						П	47	94
Утв.								

выпуск 13.11.2026 № c38d47cb31 · стр. 47 из 94

Параметры светильников для подбора

Поз.	Марки	Наименование	Установка	Кол.	P, Вт	Σ P, Вт	Ф, лм	Тц, К	Ra	Угол, °	IP	Дим.	Слой	Группа	Пом.
1	Св1, Св2, Св3, Св4, Св5, Св6, Св10, Св11, Св12, Св13, Св14, Св15, Св16, Св17, Св19, Св26, Св27, Св28, Св29, Св30, Св31, Св36, Св37, Св38, Св39, Св40, Св41, Св42, Св43	Встраиваемый точечный, встраиваемый LED-светильник, монтажная глубина ≤ 50 мм аналог по характеристикам	в ГКЛ, корпус ≤ 50 мм	29	7	203	600	3000	90	—	20	—	общий	L1, L2, L3, L6, L7, L8, L9	1, 4, 5, 6, 7
2	Св7	Бра: кронштейн — латунь брашированная, плафон-цилиндр — матовое опаловое стекло	на стене, H=1500	1	5	5	300	3000	90	—	20	—	рабочий	L1	1
3	Св60	Люстра-подвес: диск Ø600 из алебастра на трёх латунных штангах (латунь брашированная), светодиод 3000 K	подвес, низ H=2100	1	20	20	1800	3000	90	—	20	да	декоративный	L17	1
4	Св44, Св46, Св47, Св48, Св49, Св50, Св51	Встраиваемый точечный, встраиваемый LED-светильник IP44, монтажная глубина ≤ 50 мм — аналог по характеристикам	в ГКЛ, корпус ≤ 50 мм	7	7	49	600	3000	90	—	44	—	общий	L11, L13	2, 3
5	Св52, Св53, Св54, Св55, Св56, Св57	Встраиваемый точечный	в ГКЛ, корпус ≤ 50 мм	6	5	30	400	3000	90	24	20	—	акцентный	L2	4
6	Св18	Линейный настенный	под верхними шкафами, H=1400	1	30	30	2400	3000	90	—	20	—	рабочий	L4	5
7	Св63	Подвес над обеденным столом: три шара из матового стекла на общей штанге из брашированной латуни	подвес, низ H=1450	1	18	18	1600	3000	90	—	20	да	рабочий	L5	5
8	Св61	Люстра-подвес: кольцо Ø900 из брашированной латуни с плафонами из алебастра, светодиод 3000 K	подвес, низ H=2100	1	28	28	2400	3000	90	—	20	да	декоративный	L15	6
9	Св62	Картинная подсветка над картиной ДК4: латунная штанга 600, светодиод	на стене, H=1850	1	6	6	400	3000	95	—	20	да	акцентный	L16	6
10	Св58, Св59	Подвес прикроватный: штанга латунь брашированная, плафон-цилиндр Ø120 — алебастр	подвес	2	6	12	400	3000	90	—	20	—	рабочий	L10	7
		Итого		**50 шт**		**401**									

LED-ленты, линейные светильники и блоки питания


Марка	Пом.	L, м	U, В	Вт/м	Σ P, Вт	БП	P БП, Вт	Загр., %	Питание	Доступ к БП
Св18	5	3	—	—	30	у ленты	36	83	встроенный ввод	люк ревизии 300×300 мм

Примечания

1. Позиции и марки Св — те же, что на плане освещения (лист 47); группы L — по плану выключателей (лист 49).
2. Модели выбраны не у всех позиций: лист — техническое задание на подбор. Модель по строке таблицы: поток, Тц, Ra, угол, IP и регулировка яркости не хуже указанных, мощность не больше; встраиваемые — под глубину короба (графа «Установка»). IP 20 — сухие помещения. После выбора моделей (артикул, производитель) лист выпускается как «Спецификация светильников».
3. Мощность и поток в таблице — требования к подбору (поток не меньше, мощность не больше указанных); после выбора модели — по её паспорту, Σ P — установленная мощность освещения. Оценка освещённости — на плане освещения; это не светотехнический расчёт.

	Лист	№ док.	Подпись	Дата	Проект: Квартира 68 м², элитный модерн			
Дизайнер	Кырлан А.С.			13.11.26	Техническое задание на подбор светильников	Стадия	Лист	Листов
Проверил						П	48	94
Н. контр.								
Утв.								

План выключателей (М 1:50)

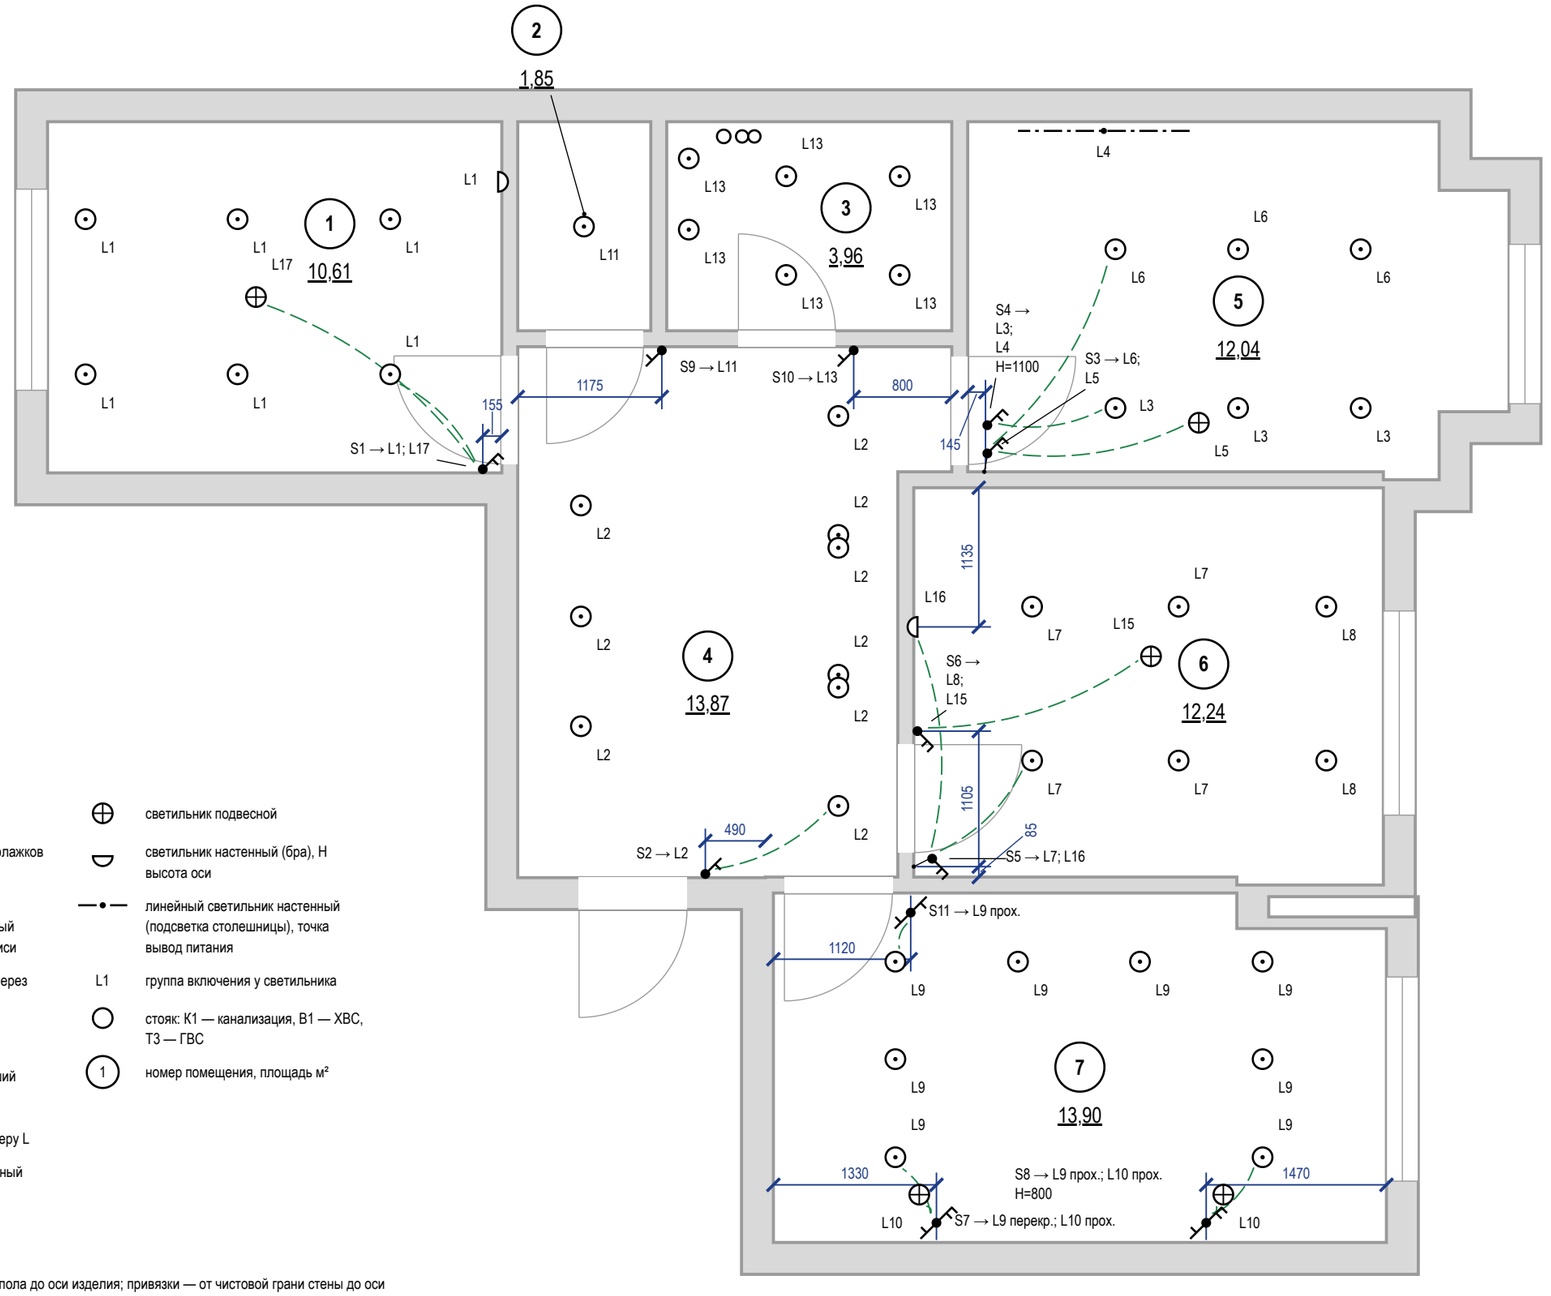

Условные обозначения


- выключатель одноклавишный
- выключатель двухклавишный (флажков — по числу клавиш)
- выключатель с проходной или перекрёстной клавишей (обратный флажок); тип клавиши — в подписи
- S1 → марка → группы по клавишам (через «;»): прох. — проходной, перекр. перекрёстный, дим. светорегулятор; Н — высота
- связь: выключатель → ближайший светильник группы в том же помещении (не трасса кабеля); полный состав группы — по номеру L
- светильник встраиваемый точечный
- светильник подвесной
- светильник настенный (бра), Н высота оси
- линейный светильник настенный (подсветка столешницы), точка вывод питания
- L1 группа включения у светильника
- стояк: К1 — канализация, В1 — ХВС, Т3 — ГВС
- 1 номер помещения, площадь м²

Примечания

1. За отметку 0,000 принят уровень чистого пола. Высоты Н — от чистого пола до оси изделия; привязки — от чистовой грани стены до оси механизма (у рамки на несколько постов — до оси рамки).
2. Высота установки, не указанная на плане: выключатели — 900 мм от чистого пола (у кровати и другие — Н у марки), со стороны дверной ручки (ПУЭ 7.1.51).
3. Какой выключатель какие светильники включает — по номеру группы L: у выключателя (S1 → L1; L2 — клавиши по порядку) и у каждого светильника. Пунктир — подсказка к ближайшему светильнику группы в том же помещении (не дальше 3 м), это не трасса кабеля; выключатель за стеной (у двери санузла) и далёкая группа — только номер группы.
4. Группы из нескольких мест (L9 — S7, S8, S11; L10 — S7, S8): на крайних местах — проходные клавиши, на промежуточных — перекрёстные; механизмы — в ведомости изделий.
5. Розеточные и мокрые линии — через УЗО или дифавтомат с током утечки не более 30 мА (ПУЭ 7.1.79); в санузле выполнить ДСУП (ПУЭ 7.1.87–7.1.88).
6. Кабель — медный, исполнение нг(А)-LS (ГОСТ 31565-2012); скрытая прокладка только горизонтально и вертикально, фактические трассы зафиксировать исполнительной схемой до закрытия отделкой.
7. Расчёт нагрузок, токов КЗ, селективности и сечений — по проекту ЭОМ организации с допуском СРО; лист задаёт состав, расположение и группы.

	Лист	№ док.	Подпись	Дата	Проект: Квартира 68 м², элитный модерн	М 1:50		
Дизайнер	Кырлан А.С.			13.11.26	Управление светильниками	Стадия	Лист	Листов
Проверил						П	49	94
Н. контр.								
Утв.								

План вентиляции (М 1:50)

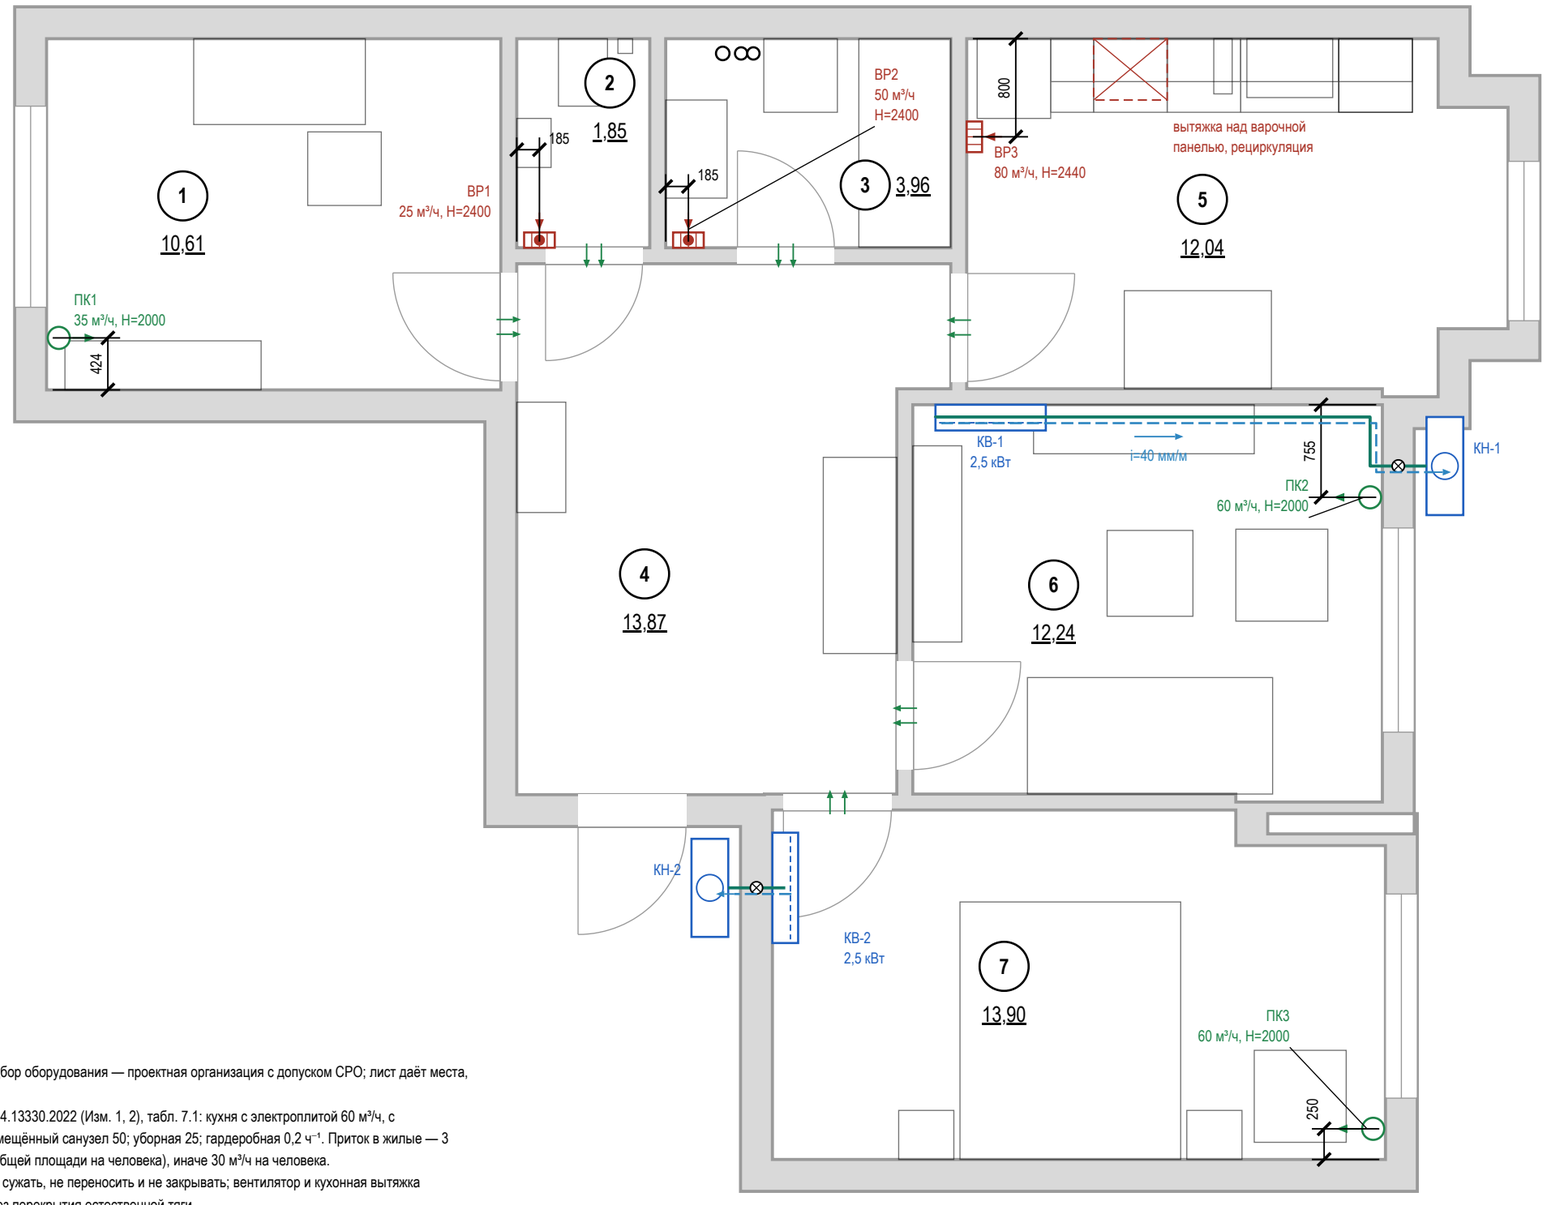

Условные обозначения

- стояк: К1 — канализация, В1 — ХВС, Т3 — ГВС
- номер помещения, площадь м²
- вытяжная решётка в вентканал: марка, расход м³/ч, Н центра от чистого пола
- вытяжная решётка с бытовым вентилятором и обратным клапаном: марка, расход, Н
- приточный клапан (КИВ) в наружной стене: марка, расход, Н центра
- переток: зазор под полотном или переточная решётка
- кухонная вытяжка над варочной панелью
- внутренний блок кондиционера (КВ-N)
- наружный блок (КН-N) на фасаде / в корзине
- трасса фреонопровода и межблочного кабеля
- дренаж конденсата (уклон стрелкой)
- отверстие в наружной стене под трассу

Воздухообмен, м³/ч

№	Помещение	Выт. норма	Выт. проект	Прит. норма	Прит. проект	Устрой-ства
1	Кабинет			32	35	ПК1
2	Санузел	25	25			ВР1
3	Ванная	50	50			ВР2
5	Кухня-столовая	60	60			ВР3
6	Гостиная			60	60	ПК2
7	Спальня			60	60	ПК3
	Итого	**135**	**135**	**152**	**155**	
	Норма по жильцам: 30×2			60		

Воздухообмен квартиры — по большей из сумм притока и вытяжки: норма 152 м³/ч, проект 155 м³/ч.
Приток больше вытяжки на 20 м³/ч — поднять вытяжку.

Кондиционеры

Марка	Помещение	Нар. блок	Трасса, м	Дренаж
КВ-1	6. Гостиная	КН-1	4,7	наружу, i=40 мм/м
КВ-2	7. Спальня	КН-2	0,8	наружу, i=40 мм/м


Привязки — до обмера
Вентканалы в исходных данных не заданы: решётки и вход вытяжки показаны у стояков К1 (вентблок у мокрой зоны). До черновых работ — обмер каналов и проверка тяги; лист перевыпустить по факту.

Примечания

1. Расчёт систем ОВ и подбор оборудования — проектная организация с допуском СРО; лист даёт места, трассы и привязки.
2. Нормы вытяжки — СП 54.13330.2022 (Изм. 1, 2), табл. 7.1: кухня с электроплитой 60 м³/ч, с газовой 100; ванная и совмещённый санузел 50; уборная 25; гардеробная 0,2 ч⁻¹. Приток в жилые — 3 м³/ч на 1 м² (менее 20 м² общей площади на человека), иначе 30 м³/ч на человека.
3. Вентканалы и шахты не сужать, не переносить и не закрывать; вентилятор и кухонная вытяжка через обратный клапан, без перекрытия естественной тяги.
4. Проектные расходы — не ниже нормы, вытяжка сведена с притоком вентиляторами мокрых помещений. Клапаны — в простенке у окна, центр 2000 мм, не над кроватью, не ближе 300 мм к стоякам отопления; типоразмер — на расход.
5. Кухня-столовая (пом. 5): вытяжка над варочной панелью рециркуляционная — без воздуховода, короба и входа в канал, в воздухообмен не включена; естественная тяга через решётку канала сохраняется. Отвод в канал — только вариантом по реестру (после обмера канала).
6. Переток — зазор под полотнами межкомнатных дверей или переточная решётка.
7. Дренаж кондиционера — непрерывный уклон 40–60 мм/м без контруклонов (СТО НОСТРОЙ 2.23.1-2011, п. 5.8.4); врезка в К1 — через сифон (п. 5.8.9); длина трассы и перепад высот — по паспорту блока; внутренний блок — не ближе 150 мм к потолку, не над кроватью и рабочим местом.
8. Наружный блок на фасаде многоквартирного дома — с согласия собственников (общее имущество); при наличии корзин — только в них. Блоки со * размещены условно.
9. Привязки оборудования — по паспортам приобретённых моделей, до черновых работ.

	Лист	№ док.	Подпись	Дата	Проект: Квартира 68 м², элитный модерн	М 1:50
Дизайнер	Кырлан А.С.			13.11.26	План вентиляции	Стадия: П; Лист: 50; Листов: 94
Проверил						
Н. контр.						
Утв.						

План отопления (М 1:50)

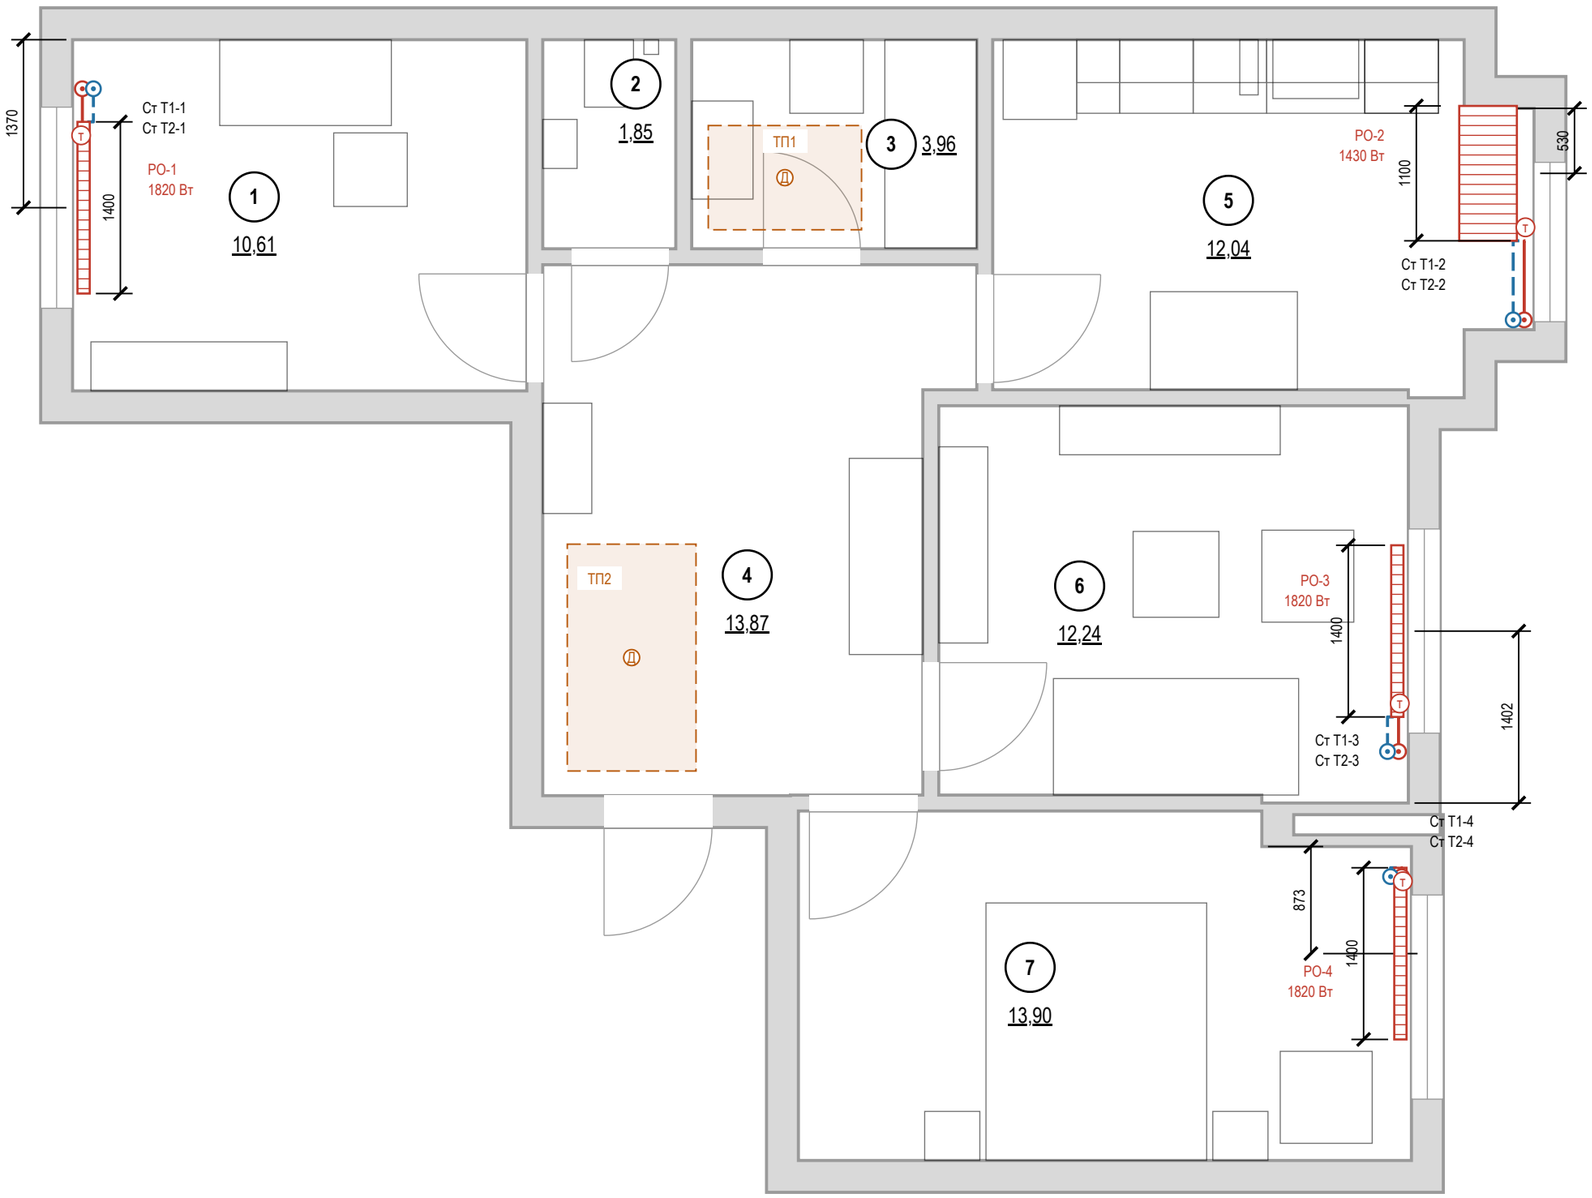

Условные обозначения

- 1 — номер помещения, площадь м²
- радиатор отопления (марка РО-N, длина по плану)
- клапан с термоголовкой на подаче
- стояк отопления, подающий (Ст Т1-N)
- стояк отопления, обратный (Ст Т2-N)
- Т1 — отопление, подающий трубопровод
- Т2 — отопление, обратный трубопровод

Ведомость радиаторов

Марка	Помещение	Тип	Д×В×Г, мм	Низ / стена	Q, Вт
РО-1	1. Кабинет	панельный 22	1400×500×100	120 / 40	1820
РО-2	5. Кухня-столовая	панельный 22	1100×500×100	120 / 40	1430
РО-3	6. Гостиная	панельный 22	1400×500×100	120 / 40	1820
РО-4	7. Спальня	панельный 22	1400×500×100	120 / 40	1820


Низ — от чистого пола, стена — зазор до задней панели, мм.

Привязки — до обмера
Стояки отопления в исходных данных не заданы: показаны у откосов окон, подводки — принципиально. До черновых работ — обмер стояков и паспорта приборов; лист перевыпустить по факту.

Примечания

1. Расчёт системы отопления, теплопотерь и подбор приборов — проектная организация с допуском СРО; лист даёт места и привязки.
2. Электрический тёплый пол: ТП1 — пом. 3, мат 1250×850 мм, 160 Вт; ТП2 — пом. 4, мат 1050×1850 мм, 290 Вт; контуры показаны пунктиром; датчик температуры (Д) — в гофротрубе, трасса к терморегулятору — по обмеру. Марка мата и точное положение датчика — при закупке и по обмеру.
3. Тип, длина и мощность радиаторов — по теплотехническому расчёту; лист задаёт места, зазоры и подключение.
4. Зазоры радиатора: низ не менее 100 мм от чистого пола, верх не менее 100 мм до подоконника, 30–50 мм от стены до задней панели; центр по оси окна с допуском ±20 мм. Верх до подоконника — 280 мм.
5. Радиаторы не закрывать глухими коробами и мебелью; перенос и замена приборов в многоквартирном доме — переустройство, согласование с управляющей организацией (ЖК РФ ст. 25–26); вынос на лоджию запрещён.
6. Трубы отопления через межквартирные стены не прокладывать (СП 51.13330.2011, п. 9.19); через перекрытия и перегородки — в гильзах.
7. Привязки приборов и подводок — по паспортам приобретённых радиаторов и клапанов, до черновых работ.
8. До закрытия отделкой трубопроводы отопления испытать гидростатическим давлением с оформлением акта (СП 73.13330.2016, 7.2–7.3).

	Лист	№ док.	Подпись	Дата	Проект: Квартира 68 м², элитный модерн	М 1:50		
Дизайнер	Кырлан А.С.			13.11.26	План отопления	Стадия	Лист	Листов
Проверил						П	51	94
Н. контр.								
Утв.								

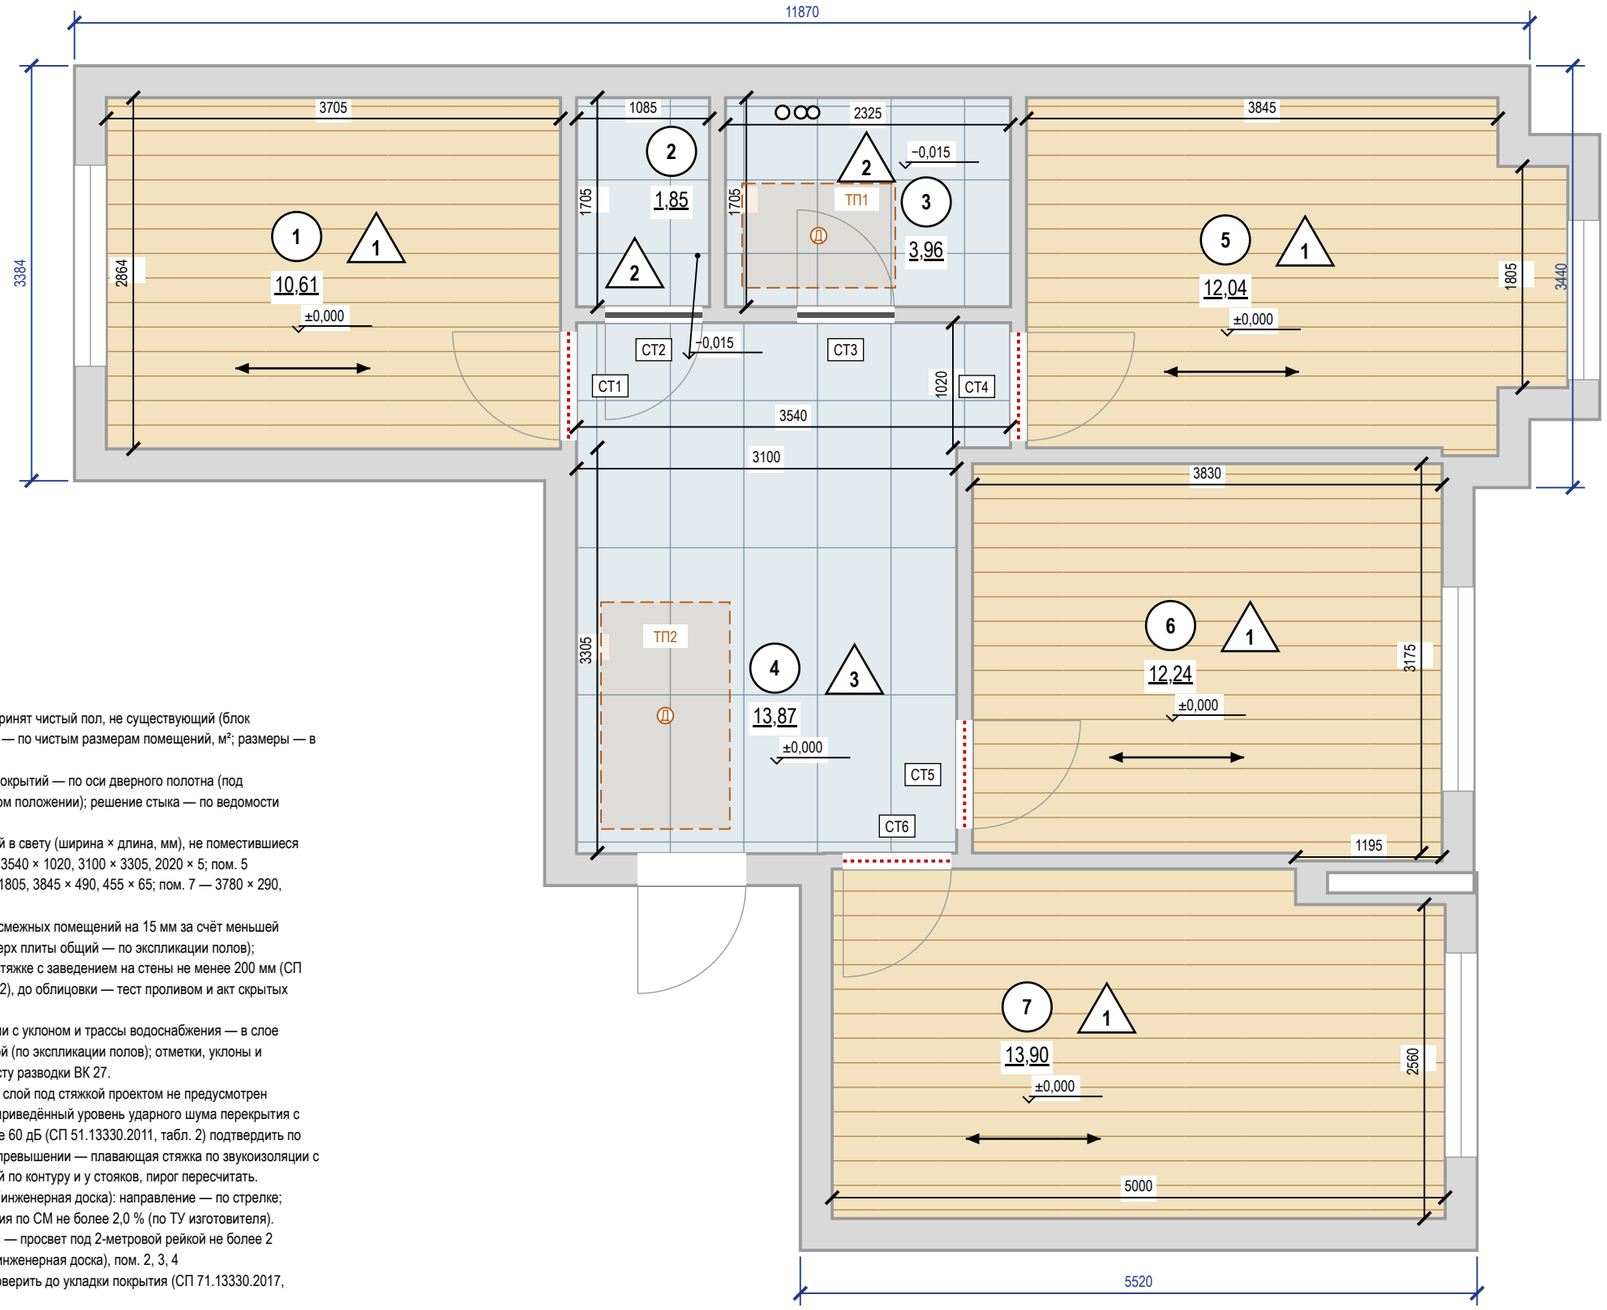

Экспликация полов

Пом.	Тип пола	Схема пола	Элементы пола, толщина, мм	Площадь, м²
1, 5, 6, 7	1		Инженерная доска на клею 14 Стяжка ЦПС М200 — 50 Плита перекрытия Всего 64 мм; ЧП ±0,000, верх плиты −0,064	48,79
2, 3	2		Керамогранит на клею С2 TE S1 — 14 Гидроизоляция обмазочная, 2 слоя, с заведением на стены 200 мм — 2 Стяжка ЦПС М200 — 33 Плита перекрытия Всего 49 мм; ЧП −0,015, верх плиты −0,064	5,81
4	3		Керамогранит на клею С2 TE S1 — 14 Стяжка ЦПС М200 — 50 Плита перекрытия Всего 64 мм; ЧП ±0,000, верх плиты −0,064	13,87
			Итого	**68,47**

Раскладка покрытий

Пом.	Укладка	Старт (оси от чистовых стен), мм	Отступ 1-го ряда / крайние плитки, мм
1	вдоль стен А/В, прямая	от стены А, 1-й ряд вдоль неё	зазор от стены не задан
2	прямая, сетка 600×600, шов 2	ось X 519 от Г; ось Y 829 от А	X 518 / 518; Y 527 / 527
3	прямая, сетка 600×600, шов 2	ось X 1139 от Г; ось Y 829 от А	X 536 / 536; Y 527 / 527
4	прямая, сетка 600×1200, шов 2	ось X 1746 от Г; ось Y 2141 от А	X 541 / 541; Y 938 / 938
5	вдоль стен А/В, прямая	от стены А, 1-й ряд вдоль неё	зазор от стены не задан
6	вдоль стен А/В, прямая	от стены А, 1-й ряд вдоль неё	зазор от стены не задан
7	вдоль стен А/В, прямая	от стены А, 1-й ряд вдоль неё	зазор от стены не задан

Спецификация плинтусов

Наименование	Помещения	Длина, м (с запасом)
Плинтус МДФ под покраску 80×16, крепление к стене, окраска в цвет Farrow & Ball No. 2003	1, 4, 5, 6, 7	71

Отметки по высоте


±0,000 чистый пол пом. 1, 4–7; отсчёт высот
−0,015 чистый пол пом. 2, 3, ниже на 15 мм
−0,064 верх плиты — расчёт, не замер (задание на обмер)
сущ. пол снимается до плиты; не замерен (задание на обмер)

Примечания


1. За отметку ±0,000 принят чистый пол, не существующий (блок отметок). Площади — по чистым размерам помещений, м²; размеры — в мм.
2. Стык разнотипных покрытий — по оси дверного полотна (под полотном в закрытом положении); решение стыка — по ведомости стыков.
3. Размеры помещений в свету (ширина × длина, мм), не поместившиеся на плане: пом. 4 — 3540 × 1020, 3100 × 3305, 2020 × 5; пом. 5 3845 × 560, 4415 × 1805, 3845 × 490, 455 × 65; пом. 7 — 3780 × 290, 5000 × 2560.
4. Пол санузлов ниже смежных помещений на 15 мм за счёт меньшей толщины стяжки (верх плиты общий — по экспликации полов); гидроизоляция по стяжке с заведением на стены не менее 200 мм (СП 29.13330.2011, п. 7.2), до облицовки — тест проливом и акт скрытых работ.
5. Выпуски канализации с уклоном и трассы водоснабжения — в слое засыпки под стяжкой (по экспликации полов); отметки, уклоны и прочистки — по листу разводки ВК 27.
6. Звукоизоляционный слой под стяжкой проектом не предусмотрен (стяжка по плите): приведённый уровень ударного шума перекрытия с полом Lnw не более 60 дБ (СП 51.13330.2011, табл. 2) подтвердить по данным дома; при превышении — плавающая стяжка по звукоизоляции с демпферной лентой по контуру и у стояков, пирог пересчитать.
7. Штучные покрытия (инженерная доска): направление — по стрелке; влажность основания по СМ не более 2,0 % (по ТУ изготовителя).
8. Ровность основания — просвет под 2-метровой рейкой не более 2 мм: пом. 1, 5, 6, 7 (инженерная доска), пом. 2, 3, 4 (керамогранит); проверить до укладки покрытия (СП 71.13330.2017, табл. 8.5).
9. Сетка на плитке — условная, в размер формата; точка старта и раскладка — по листу раскладки плитки.
10. Узор покрытия (заливка-код типа пола) прерывается под надписями — площадями помещений и отметками чистого пола.
11. Электрический тёплый пол: ТП1 — пом. 3, мат 1250×850 мм, 160 Вт; ТП2 — пом. 4, мат 1050×1850 мм, 290 Вт; контуры показаны пунктиром; датчик температуры (Д) — в гофротрубе, трасса к терморегулятору — по обмеру. Марка мата и точное положение датчика — при закупке и по обмеру.
12. Пироги полов — по экспликации полов: слои сверху вниз, толщины в мм; гидроизоляция мокрых зон — в пироге и в ведомости отделки; схема пола — без масштаба.

	Лист	№ док.	Подпись	Дата	Проект: Квартира 68 м², элитный модерн	М 1:50
Дизайнер	Кырлан А.С.			13.11.26		
Проверил					План покрытий пола	Стадия П · Лист 52 · Листов 94
Н. контр.						
Утв.						


Фрагмент 1. Санузел (пом. 2). Пол 600×600, шов 2 мм (М 1:50)

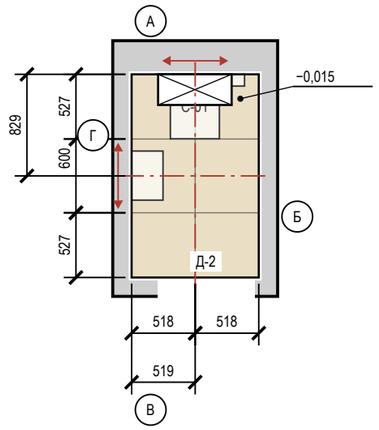

Фрагмент 2. Ванная (пом. 3). Пол 600×600, шов 2 мм (М 1:50)

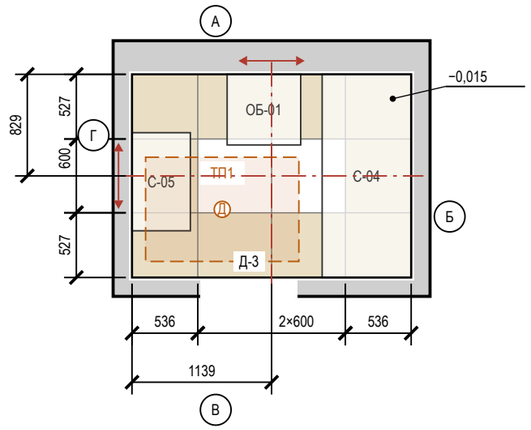

Фрагмент 3. Прихожая (пом. 4). Пол 600×1200, шов 2 мм (М 1:50)

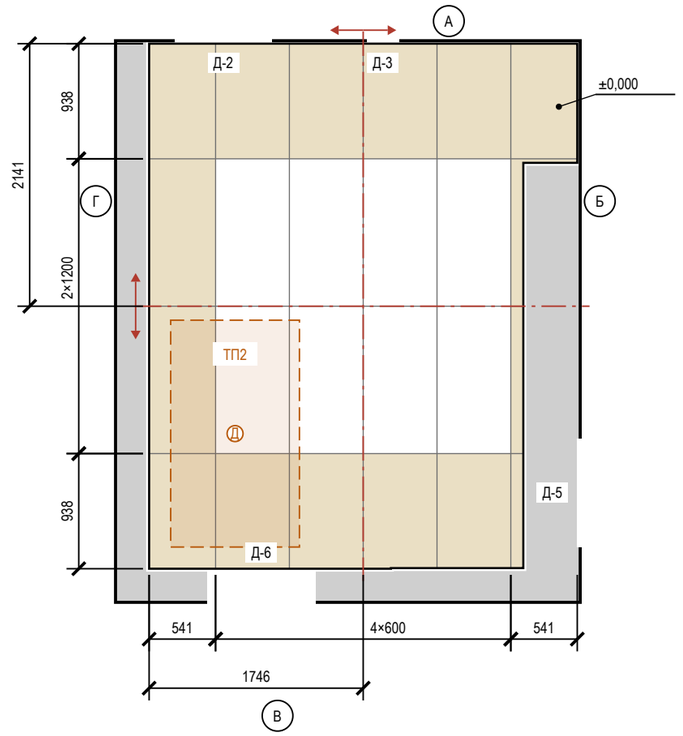

Условные обозначения

- плитка целая; тонкая линия — шов
- плитка с подрезкой (размер — на цепочке)
- ось старта; стрелки — направление укладки
- сантехприбор: габарит, высота по практике
- короб инсталляции: плитка пола — до короба
- электрический тёплый пол: контур мата ТП, Д — датчик
- отметка чистого пола на полке выноски, м
- А — обозначение стены А–Г (как на развёртках)

Примечания

1. Раскладка от чистовых размеров: стены санузлов теряют 10 + 5 + 9 = 24 мм на сторону (штукатурка, клей, плитка); подрезки — чистые, без шва.
2. Старт — от центра помещения (штрихпунктир, стрелки — направление укладки); размер старта — от чистовых стен Г и А.
3. Раскладка фартука «Кухня-столовая» — на листе «Раскладка плитки. Фартук кухни».
4. Калибр партии не задан — до укладки замерить (рабочий размер W, ГОСТ 13996-2019) и пересчитать подрезки.
5. Количество: целые по раскладке + по одной на подрезку, запас 10 %; один артикул — одна партия и тон. Исключены поддон, короб, проёмы и места за коробом; S — по чистым граням: стены нетто = зона облицовки по ведомости отделки − место за коробом инсталляции 0,72 м² (плитку за коробом не кладут), короб — отдельной строкой.
6. Клей C2 TE S1 Ceresit CM 17; C2 TE S1 (ГОСТ Р 56387-2018), затирка CG2WA Mapei Ultracolor Plus 132; CG2WA; расход — по ТУ выбранной марки.
7. Гидроизоляция: пол и стены 200 мм от ЧП; над ванной — до 2000 и 300 мм за борт (пом. 3) (см. развёртки); акт скрытых работ, пролив 24 ч.
8. Электрический тёплый пол: ТП1 — пом. 3, мат 1250×850 мм, 160 Вт; ТП2 — пом. 4, мат 1050×1850 мм, 290 Вт; контуры показаны пунктиром; датчик температуры (Д) — в гофротрубе, трасса к терморегулятору — по обмеру. Марка мата и точное положение датчика — при закупке и по обмеру. Плитку над матом клеить клеем, который изготовитель допускает для тёплого пола, до включения выдержать срок по ТУ клея.
9. Швы пола совмещены со швами стены А; по периметру — демпферная лента.
10. Отметка чистого пола −0,015, порог 15 мм; стык с соседним покрытием — по оси полотна двери.

Ведомость плитки

Помещение, поверхность	Плитка, код	Формат	Шов	S, м²	Целых	Подр.	С запасом
Санузел, пол	аналог: керамогранит под травертин	600×600	2	1,85	0	6	7
Санузел, стены А–Г	аналог: керамогранит под травертин	600×1200	2	11,04	4	16	24
Санузел, короб инсталляции	аналог: керамогранит под травертин	600×1200	2	1,47	1	3	5
Ванная, пол	аналог: керамогранит под травертин	600×600	2	3,96	2	10	14
Ванная, стены А–Г	аналог: керамогранит под травертин	600×1200	2	17,72	8	20	32
Прихожая, пол	аналог: керамогранит ректифицированный под травертин, матовый	600×1200	2	13,87	8	16	27
Кухня-столовая, фартук (ст. А)	аналог: керамогранит под травертин, матовый	1200×600	2	1,68	0	5	6
Итого 600×600				5,81	2	16	21
Итого 600×1200				**45,78**	**21**	**60**	**94**


Ведомость материалов

Материал	Класс, код	Норма расхода	Кол-во
Затирка	CG2WA Mapei Ultracolor Plus 132	(a+b)/ab·шов·t·1,6	4,0 кг
Затирка	CG2WA	(a+b)/ab·шов·t·1,6	0,1 кг
Клей	C2 TE S1 Ceresit CM 17	1,2 кг/м²·мм, слой 5	318 кг (13 меш.)
Клей	C2 TE S1	1,2 кг/м²·мм, слой 5	12 кг (1 меш.)
Гидроизоляция	обмазочная, 2 слоя: пол, стены по периметру и зоны замачивания	по ТУ	15,8 м²
Демпф. лента	по периметру пола из плитки		26,9 м

	Лист	№ док.	Подпись	Дата	Проект: Квартира 68 м², элитный модерн			М 1:50
Дизайнер	Кырлан А.С.			13.11.26	Раскладка плитки. Планы полов	Стадия	Лист	Листов
Проверил						П	53	94
Н. контр.								
Утв.								

выпуск 13.11.2026 № c38d47cb31 · стр. 53 из 94

Фрагмент 1. Кухня-столовая (пом. 5), фартук, стена А. 1200×600, шов 2 мм (М 1:20)

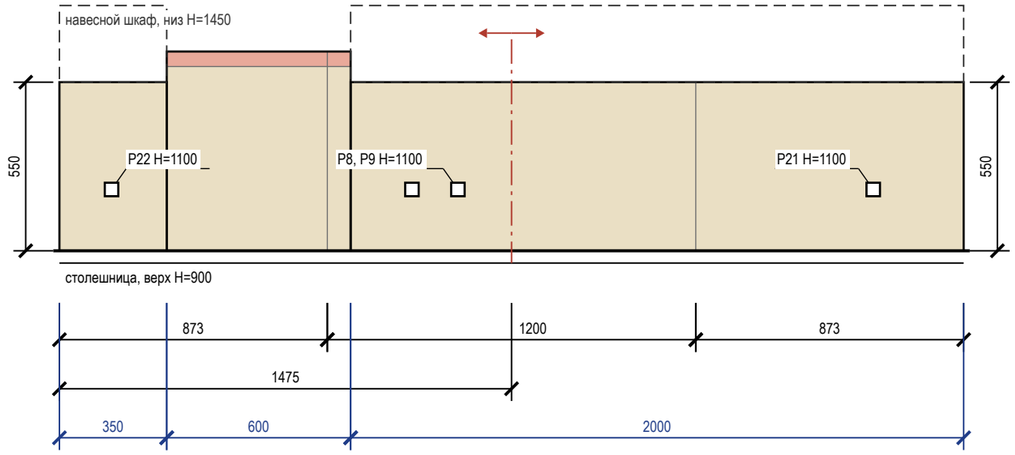

Условные обозначения

- плитка целая; тонкая линия — шов
- плитка с подрезкой (размер — на цепочке)
- ось старта; стрелки — направление укладки
- электроточка: марка и H — по листам ЭОМ
- столешница (верх)
- навесной шкаф над фартуком

Подсчёт плитки

Поверхность	Формат	S, м²	Целых	Подр.	С запасом
Кухня-столовая, фартук (ст. А)	1200×600	1,68	0	5	6

Сдвиг розеток фартука под раскладку


Точка (ЭОМ)	Сейчас: от края фартука / H	Под раскладку: от края / H	Сдвиг, мм
P8, P9, P22	1150, 1300, 170 / 1100	1150, 1300, 170 / 1175	H +75 — ось ряда
P21	2655 / 1100	2655 / 1175	H +75 — ось ряда

Примечания

1. Фартук, Кухня-столовая: 1200×600 горизонтально, шов 2 мм; зоны 350 мм — 900…1450, 600 мм — 900…1550, 2000 мм — 900…1450 (от столешницы до низа навесного шкафа, без шкафа — 650 мм). Старт от центра участка, подрезки 873 мм. Площадь 1,68 м² — как в ведомости отделки.
2. Фартук — после монтажа столешницы, низ на 2–3 мм выше неё, шов со столешницей — санитарный герметик; навесные шкафы — после фартука. Торцы у пенала и стены — профиль или запил 45°.
3. Фартук, Кухня-столовая: в зоне до отм. 1550 верхний ряд подрезан 48 мм — меньше 1/3 плитки; полоса прикрыта корпусом навесного модуля и на виду не остаётся. Раскладкой не снимается: убрать подрезку можно, только выровняв низ этого модуля с соседними (1450 мм) — решение мебельщика.
4. Розетки из таблицы переносятся до черновой электрики: по высоте — на ось ряда плитки, от вертикального шва крупной плитки — не ближе 60 мм. Привязка — от левого края фартука на развёртке.
5. Клей, затирка и итог по форматам — в ведомостях листа «Раскладка плитки. Планы полов».


	Лист	№ док.	Подпись	Дата	Проект: Квартира 68 м², элитный модерн			М 1:20
Дизайнер	Кырлан А.С.			13.11.26	Раскладка плитки. Фартук кухни	Стадия	Лист	Листов
Проверил						П	54	94
Н. контр.								
Утв.								

Стена А (М 1:25)

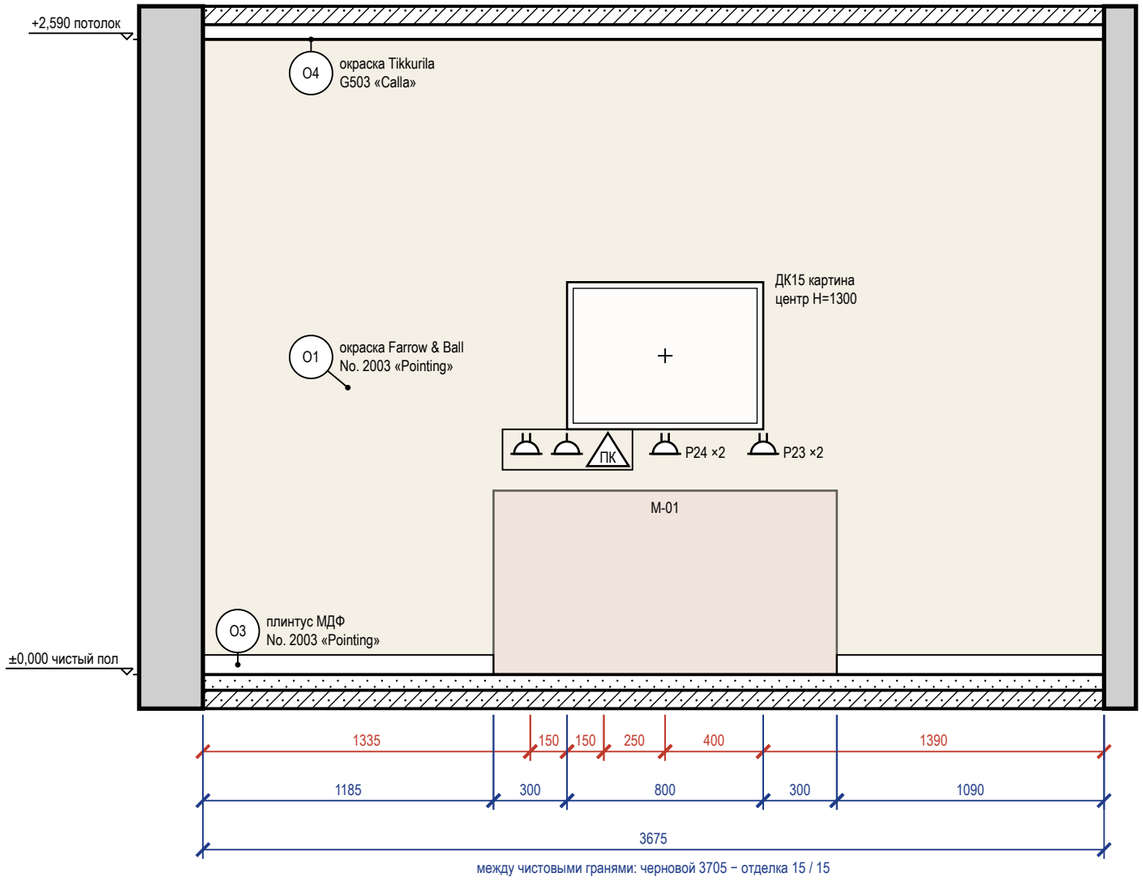

между чистовыми гранями: черновой 3705 − отделка 15 / 15

Стена Б (М 1:25)

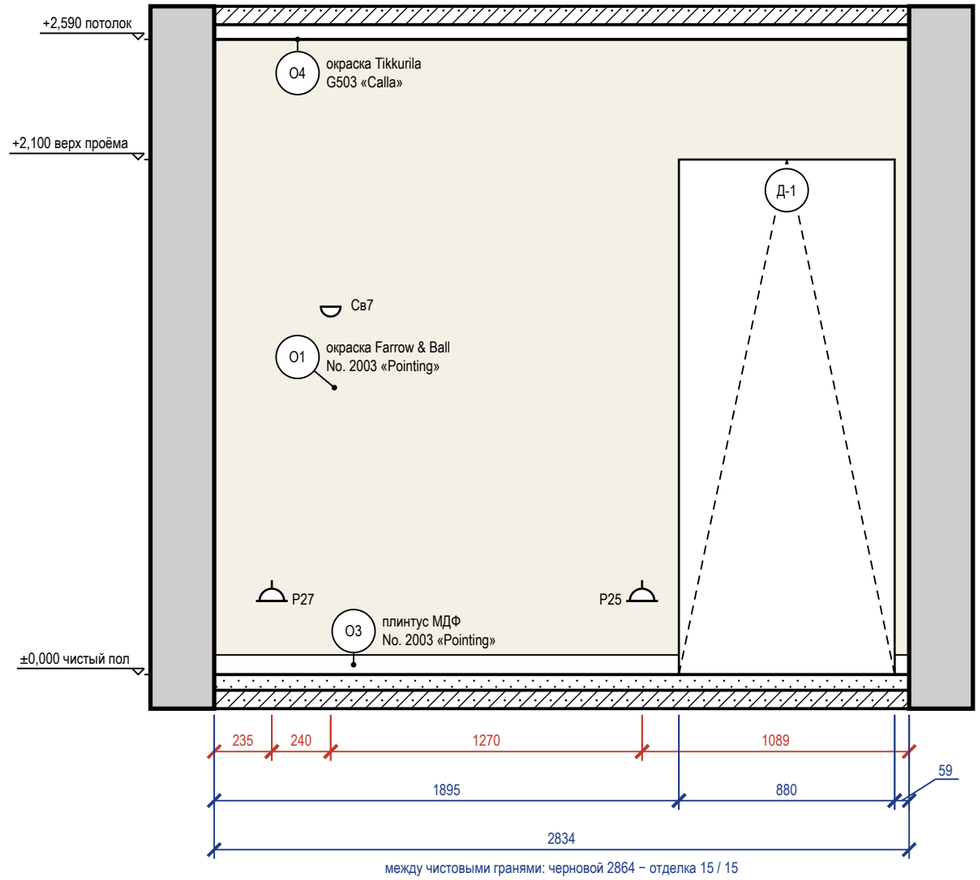

между чистовыми гранями: черновой 2864 − отделка 15 / 15


Ведомость точек и выводов

Стена	Марка	Что это	Гр.	Н, мм	От угла, мм	Примечание
А	Р1	розетка: рабочий стол	3	900	1335	рамка 2 поста
А	Р2	розетка: рабочий стол: монитор	3	900	1485	
А	LAN1	розетка RJ45: рабочий стол		900	1635	
А	Р24	розетка: рабочий стол: компьютер, монитор, зарядки	3	900	1885	рамка 2 поста
А	Р23	розетка: рабочий стол: компьютер, монитор, зарядки	3	900	2285	рамка 2 поста
Б	Р27	розетка: общего назначения	3	300	235	
Б	Св7	светильник настенный: марка 12 по исходному плану	1	1500	475	
Б	Р25	розетка: уборка у входа	3	300	1745	

Ведомость отделки (на листе)

Марка	Поверхность	Материал, изделие	Цвет, код	Кол.
О1	стены	окраска, Farrow & Ball Modern Emulsion, матовая, подготовка Q3	Farrow & Ball No. 2003 «Pointing»	15 м²
О3	плинтус	плинтус МДФ, h 80 мм, аналог: плинтус МДФ под покраску 80×16	Farrow & Ball No. 2003 «Pointing»	4,2 м
О4	потолок	окраска, Tikkurila Euro Power 7, глубокоматовая, подготовка Q3	Tikkurila G503 «Calla»	10,6 м²

Схема развёрток (М 1:50)

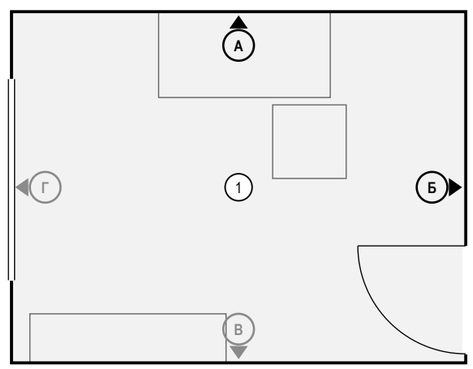


Примечания

1. Размеры — в мм от чистовых поверхностей стен; условные обозначения и общие указания — лист 12.
2. Картины и зеркала крепить к основанию по паспорту изделия (закладные и анкеры — в перечне скрытых работ); крест — ось центра предмета.
3. Часть марок не уместилась у знаков: коды, высоты и привязки этих позиций — в ведомости точек и выводов под видами.

	Лист	№ док.	Подпись	Дата	Проект: Квартира 68 м², элитный модерн		М 1:25	
Дизайнер	Кырлан А.С.			13.11.26	Развёртки стен А, Б. Кабинет (пом. 1)	Стадия	Лист	Листов
Проверил						П	55	94
Н. контр.								
Утв.								


выпуск 13.11.2026 № c38d47cb31 · стр. 55 из 94

Стена В (М 1:25)

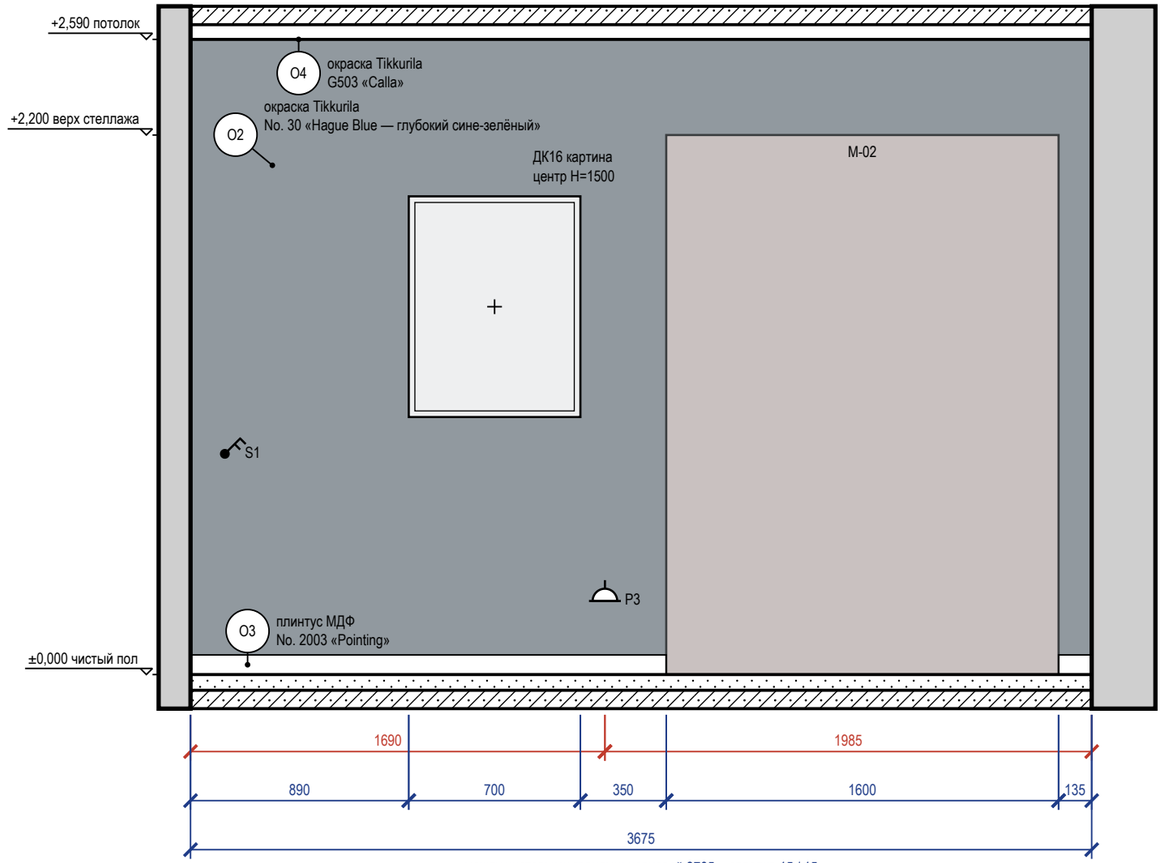

между чистовыми гранями: черновой 3705 − отделка 15 / 15

Стена Г (М 1:25)

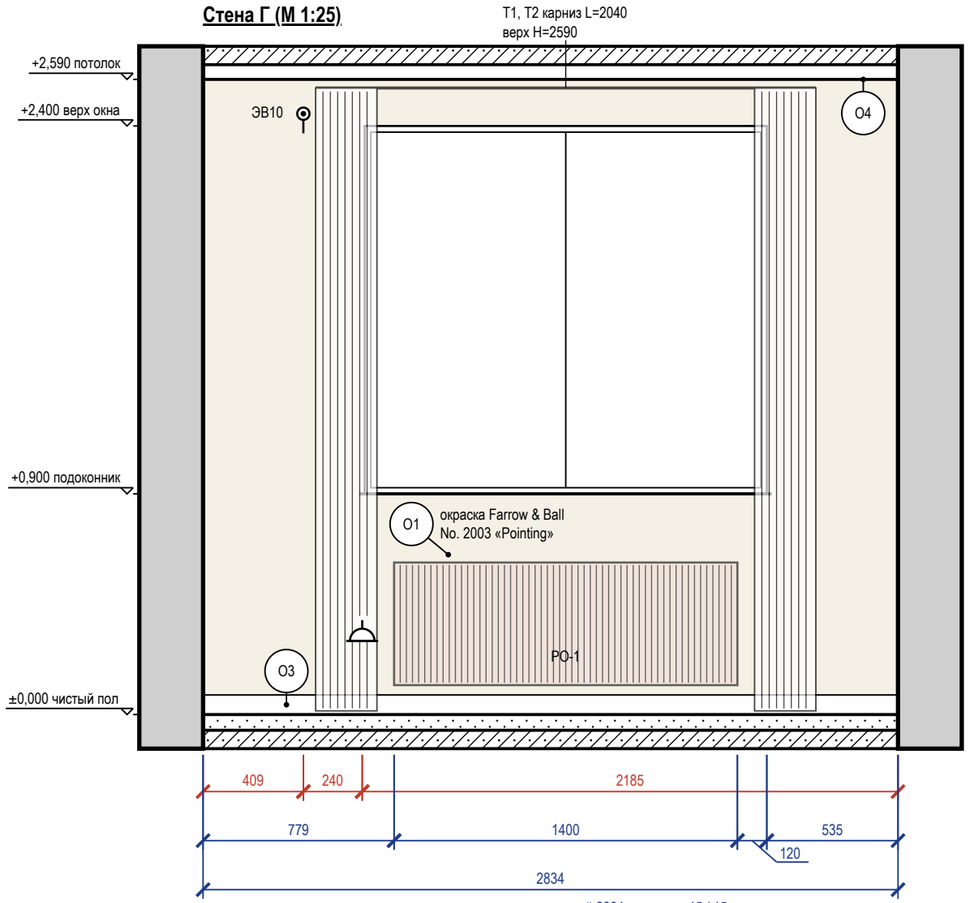


между чистовыми гранями: черновой 2864 − отделка 15 / 15


Ведомость точек и выводов

Стена	Марка	Что это	Гр.	H, мм	От угла, мм	Примечание
В	S1	выключатель	1	900	140	
В	P3	розетка: уборка	3	300	1690	
Г	ЭВ10	вывод кабеля: электрокарниз (привод штор)	3	2450	409	
Г	P26	розетка: общего назначения	3	300	649	

Схема развёрток (М 1:200)

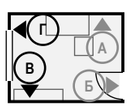

Стена Г — визуализация, лист 3

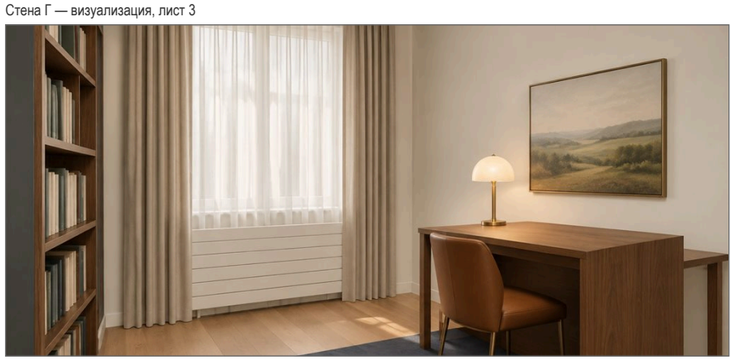

Ведомость отделки (на листе)


Марка	Поверхность	Материал, изделие	Цвет, код	Кол.
O1	стены	окраска, Farrow & Ball Modern Emulsion, матовая, подготовка Q3	Farrow & Ball No. 2003 «Pointing»	4,9 м²
O2	акцентная стена	окраска, Tikkurila Euro Power 7, колеровка по NCS, матовая, подготовка Q3	Farrow & Ball No. 30 «Hague Blue глубокий сине-зелёный»	9,5 м²
O3	плинтус	плинтус МДФ, h 80 мм, аналог: плинтус МДФ под покраску 80×16	Farrow & Ball No. 2003 «Pointing»	4,9 м
O4	потолок	окраска, Tikkurila Euro Power 7, глубокоматовая, подготовка Q3	Tikkurila G503 «Calla»	10,6 м²

Примечания


1. Размеры — в мм от чистовых поверхностей стен; условные обозначения и общие указания — лист 12.
2. Картины и зеркала крепить к основанию по паспорту изделия (закладные и анкеры — в перечне скрытых работ); крест — ось центра предмета.
3. Карнизы (шины) — по ведомости текстиля декоратора: длина L и верх H на развёртке — те же числа, что в ведомости; крепление — до окраски потолка.
4. Линии узора (швы плитки, складки штор, рёбра радиаторов) прерываются у знаков и выносок — просвет между линиями не менее 0,7 мм.
5. Часть марок не уместилась у знаков: коды, высоты и привязки этих позиций — в ведомости точек и выводов под видами.

	Лист	№ док.	Подпись	Дата	Проект: Квартира 68 м², элитный модерн			М 1:25
Дизайнер	Кырлан А.С.			13.11.26	Развёртки стен В, Г. Кабинет (пом. 1)	Стадия	Лист	Листов
Проверил						П	56	94
Н. контр.								
Утв.								

Стена А (М 1:20)

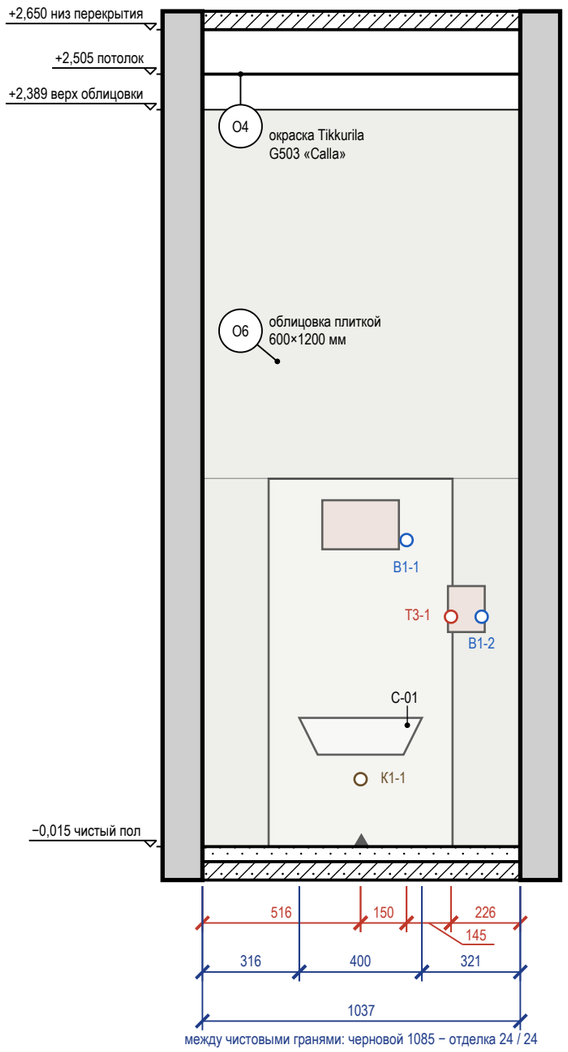


Стена Б (М 1:20)

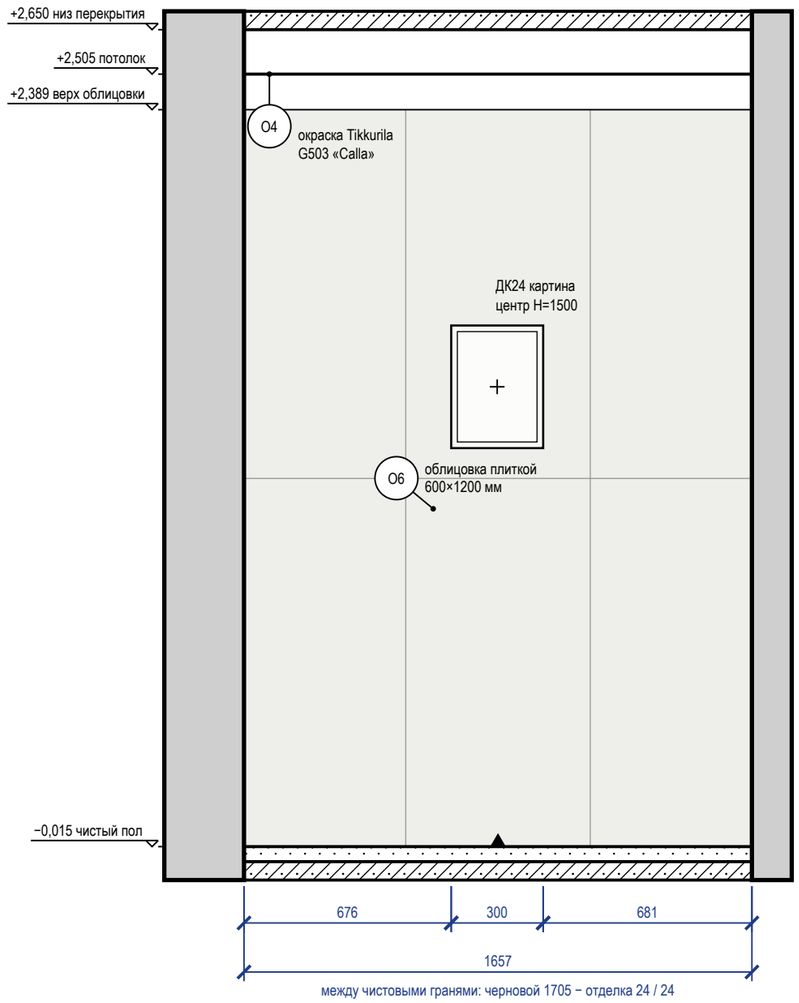

Ведомость точек и выводов

Стена	Марка	Что это	Гр.	Н, мм	От угла, мм	Примечание
А	К1-1	канализация — унитаз подвесной		220	516	Ø110
А	В1-1	холодная вода — унитаз подвесной		1000	666	в раме инсталляции
А	Т3-1	горячая вода — гигиенический душ		750	811	межос. 100
А	В1-2	холодная вода — гигиенический душ		750	911	межос. 100


Стена А — визуализация, лист 4

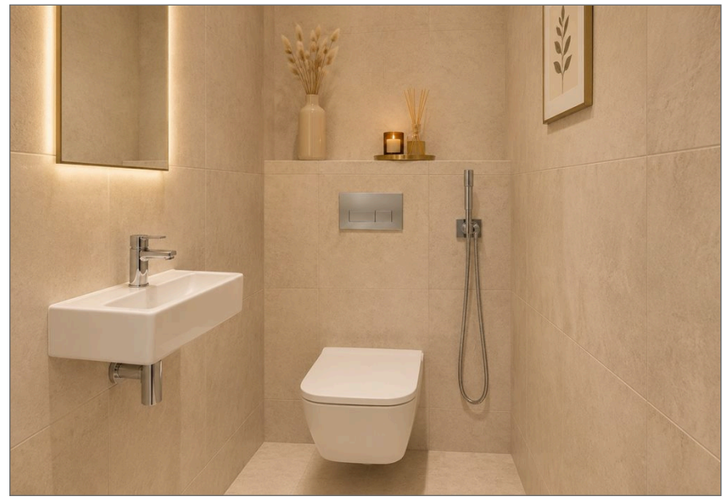

Ведомость отделки (на листе)

Марка	Поверхность	Материал, изделие	Цвет, код	Кол.
О4	потолок	окраска, Tikkurila Euro Power 7, матовая, подготовка Q3	Tikkurila G503 «Calla»	1,9 м²
О6	стены	облицовка плиткой, 600×1200×9 мм, аналог: керамогранит под травертин, матовый, затирка CG2WA		6,5 м²

Схема развёрток (М 1:50)

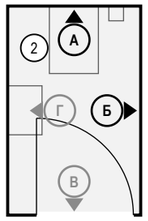

Ведомость изделий и проёмов (на листе)


Стена	Марка	Изделие, проём	На виде Ш×В, мм	Низ, мм
А	С-01	унитаз подвесной безободковый, инсталляция	400×120	300
А	С-02	гигиенический душ: лейка на держателе, смеситель скрытого монтажа с рычагом	120×150	700
Б	ДК24	картина	300×400	1300

Примечания


1. Размеры — в мм от чистовых поверхностей стен; условные обозначения и общие указания — лист 12.
2. Схема мебели, приборов и декора не является технической документацией для производства мебели; габариты — по паспортам изделий.
3. Облицовка — по сетке швов 2 мм, раскладка от оси стены (треугольник у пола), целые ряды от пола; подрезки — по листу раскладки плитки.
4. Гидроизоляция в 2 слоя, заход на стены 200 мм — до облицовки, с актом скрытых работ и тестом проливом (узел — на листе узлов).
5. Картины и зеркала крепить к основанию по паспорту изделия (закладные и анкеры — в перечне скрытых работ); крест — ось центра предмета.

	Лист	№ док.	Подпись	Дата	Проект: Квартира 68 м², элитный модерн	М 1:20		
Дизайнер	Кырлан А.С.			13.11.26	Развёртки стен А, Б. Санузел (пом. 2)	Стадия	Лист	Листов
Проверил						П	57	94
Н. контр.								
Утв.								

Стена В (М 1:20)

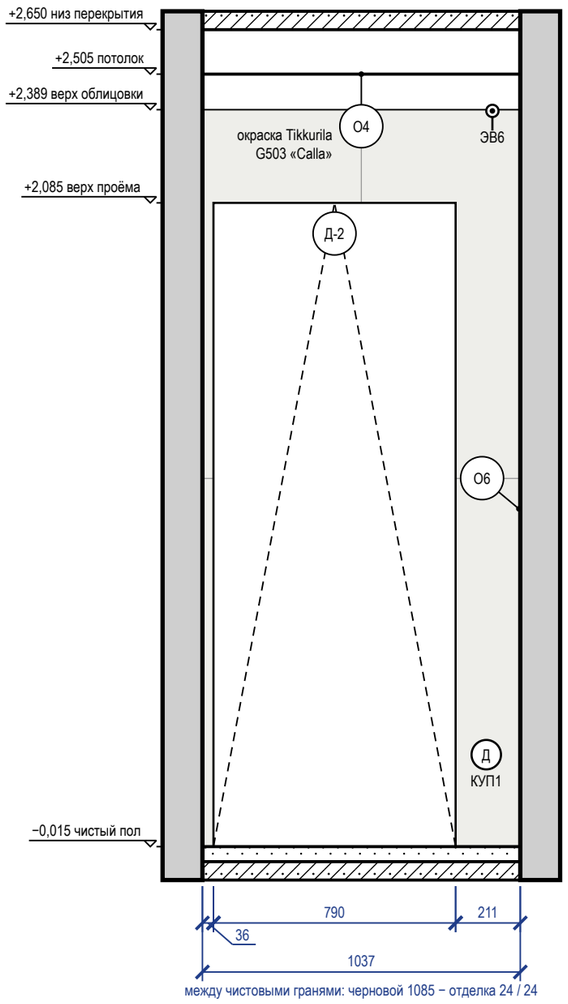

Стена Г (М 1:20)

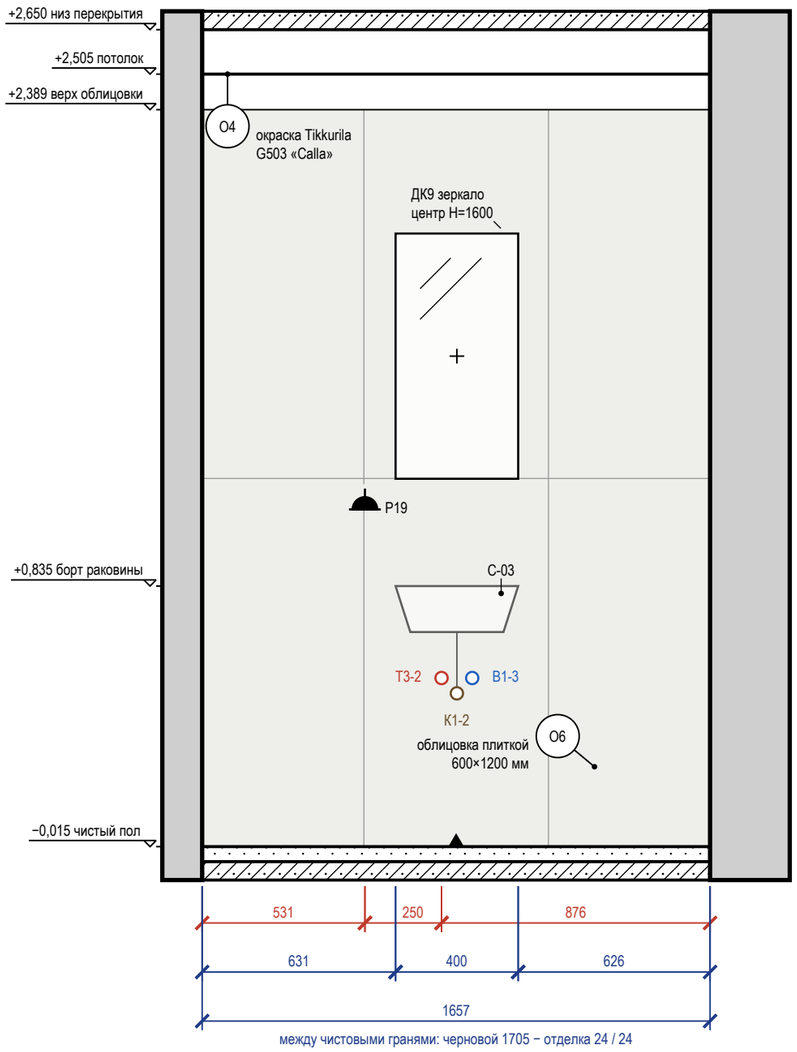


Ведомость точек и выводов

Стена	Марка	Что это	Гр.	Н, мм	От угла, мм	Примечание
В	КУП1	КУП (уравнивание потенциалов): КУП уравнивание потенциалов (ДСУП)		300	926	
В	ЭВ6	вывод кабеля: вентилятор в потолке (знак 11 по исходному плану; вывод — в запотолочное пространство) ВР1 (клавиша L11, таймер выбега)	2	2400	946	
Г	Р19	розетка: розетка у раковины (фен, зона 3)	15	1100	531	IP44
Г	Т3-2	горячая вода — умывальник		550	781	межос. 100
Г	К1-2	канализация — умывальник		500	831	Ø40
Г	В1-3	холодная вода — умывальник		550	881	межос. 100

Ведомость отделки (на листе)

Марка	Поверхность	Материал, изделие	Цвет, код	Кол.
О4	потолок	окраска, Tikkurila Euro Power 7, матовая, подготовка Q3	Tikkurila G503 «Calla»	1,9 м²
О6	стены	облицовка плиткой, 600×1200×9 мм, аналог: керамогранит под травертин, матовый, затирка CG2WA		4,8 м²

Схема развёрток (М 1:50)

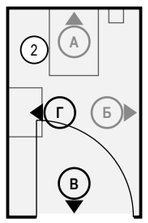

Ведомость изделий и проёмов (на листе)

Стена	Марка	Изделие, проём	На виде Ш×В, мм	Низ, мм
В	Д-2	дверь	790×2100	0
Г	С-03	раковина компактная 400 × 280 подвесная	400×150	700
Г	ДК9	зеркало	400×800	1200


Примечания

1. Размеры — в мм от чистовых поверхностей стен; условные обозначения и общие указания — лист 12.
2. Облицовка — по сетке швов 2 мм, раскладка от оси стены (треугольник у пола), целые ряды от пола; подрезки — по листу раскладки плитки.
3. Гидроизоляция в 2 слоя, заход на стены 200 мм — до облицовки, с актом скрытых работ и тестом проливом (узел — на листе узлов).
4. Картины и зеркала крепить к основанию по паспорту изделия (закладные и анкеры — в перечне скрытых работ); крест — ось центра предмета.
5. Линии узора (швы плитки, складки штор, рёбра радиаторов) прерываются у знаков и выносок — просвет между линиями не менее 0,7 мм.


	Лист	№ док.	Подпись	Дата	Проект: Квартира 68 м², элитный модерн			М 1:20
Дизайнер	Кырлан А.С.			13.11.26	Развёртки стен В, Г. Санузел (пом. 2)	Стадия	Лист	Листов
Проверил						П	58	94
Н. контр.								
Утв.								

выпуск 13.11.2026 № c38d47cb31 · стр. 58 из 94

Стена А (М 1:25)

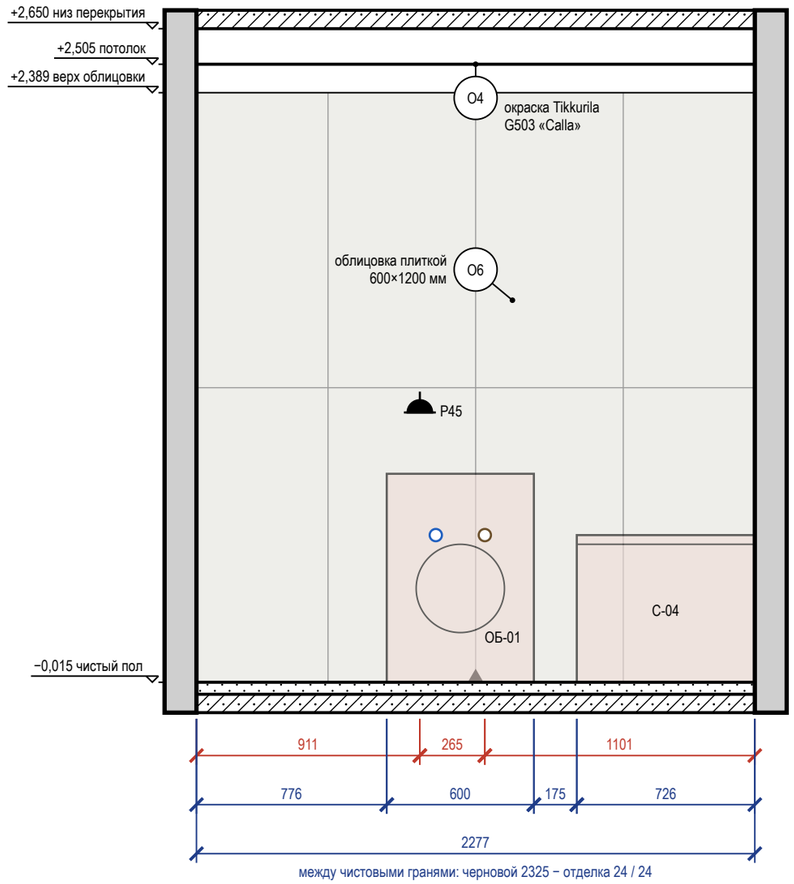

Стена Б (М 1:25)

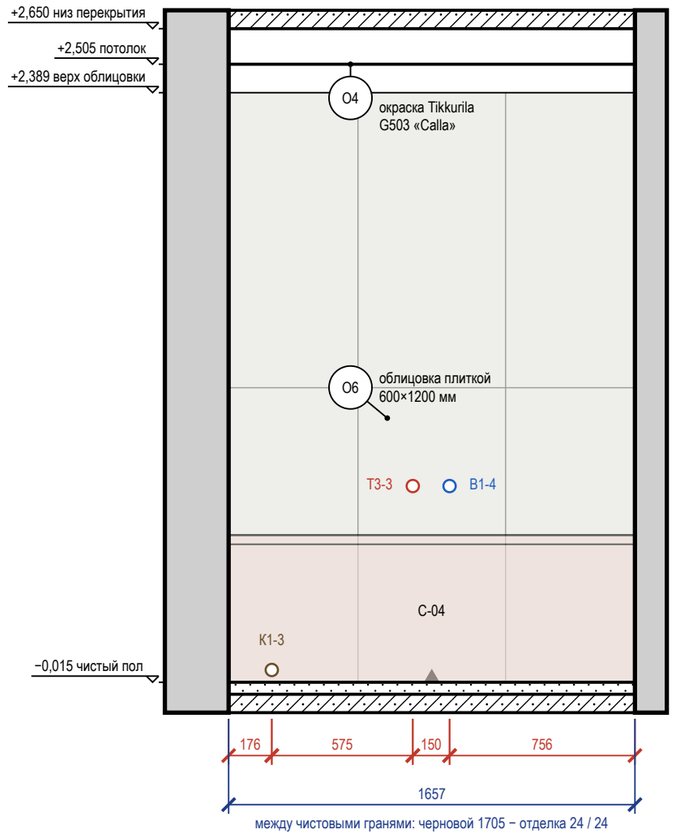


Ведомость точек и выводов

Стена	Марка	Что это	Гр.	Н, мм	От угла, мм	Примечание
А	Р45	розетка: стиральная машина	20	1100	911	IP44
А	В1-6	холодная вода — стиральная машина		600	976	кран машины
А	К1-5	канализация — стиральная машина		600	1176	Ø40
Б	К1-3	канализация — ванна		50	176	Ø50
Б	Т3-3	горячая вода — ванна		800	751	межос. 150
Б	В1-4	холодная вода — ванна		800	901	межос. 150

Стена А — визуализация, лист 6




Стена Б — визуализация, лист 7

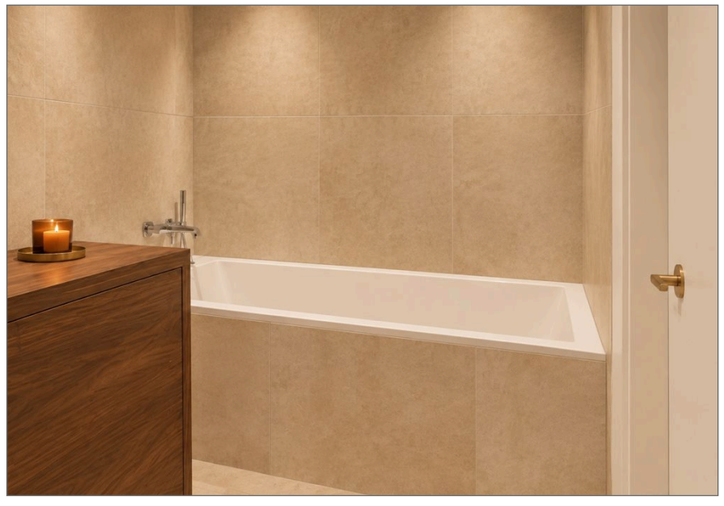

Ведомость отделки (на листе)

Марка	Поверхность	Материал, изделие	Цвет, код	Кол.
О4	потолок	окраска, Tikkurila Euro Power 7, матовая, подготовка Q3	Tikkurila G503 «Calla»	4 м²
О6	стены	облицовка плиткой, 600×1200×9 мм, аналог: керамогранит под травертин, матовый, затирка CG2WA		9,5 м²

Схема развёрток (М 1:50)

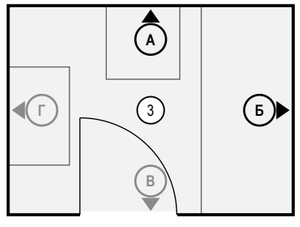


Примечания

1. Размеры — в мм от чистовых поверхностей стен; условные обозначения и общие указания — лист 12.
2. Облицовка — по сетке швов 2 мм, раскладка от оси стены (треугольник у пола), целые ряды от пола; подрезки — по листу раскладки плитки.
3. Гидроизоляция в 2 слоя, заход на стены 200 мм; над ванной — до 2000 и 300 мм за борт — до облицовки, с актом скрытых работ и тестом проливом (узел — на листе узлов).
4. Часть марок не уместилась у знаков: коды, высоты и привязки этих позиций — в ведомости точек и выводов под видами.

	Лист	№ док.	Подпись	Дата	Проект: Квартира 68 м², элитный модерн	М 1:25		
Дизайнер	Кырлан А.С.			13.11.26	Развёртки стен А, Б. Ванная (пом. 3)	Стадия	Лист	Листов
Проверил						П	59	94
Н. контр.								
Утв.								


выпуск 13.11.2026 № c38d47cb31 · стр. 59 из 94

Стена В (М 1:25)

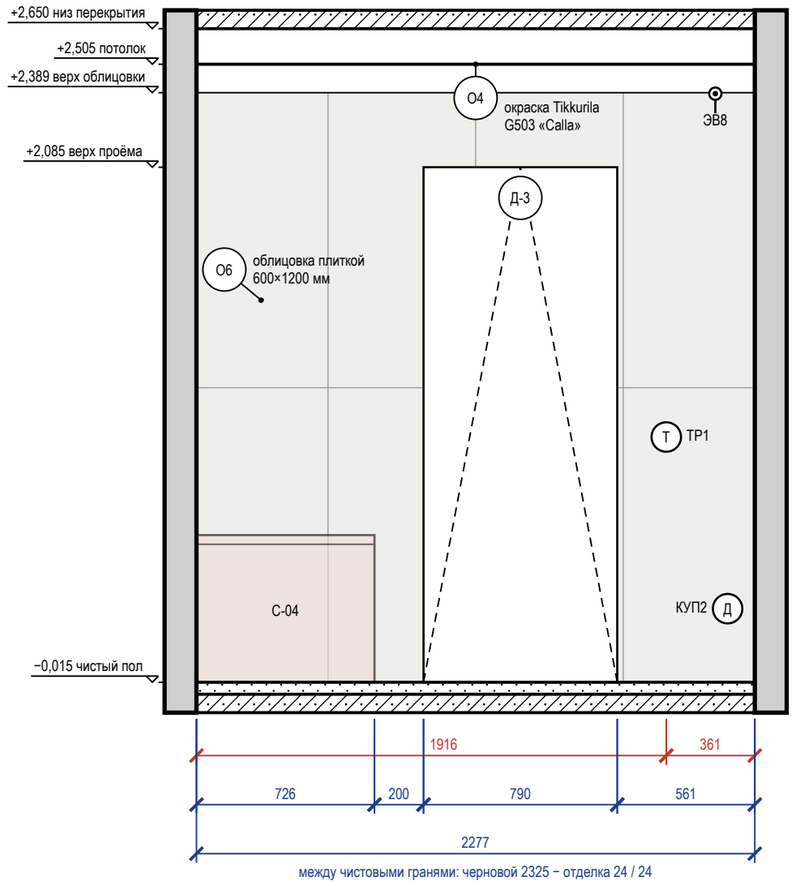

между чистовыми гранями: черновой 2325 − отделка 24 / 24

Стена Г (М 1:25)

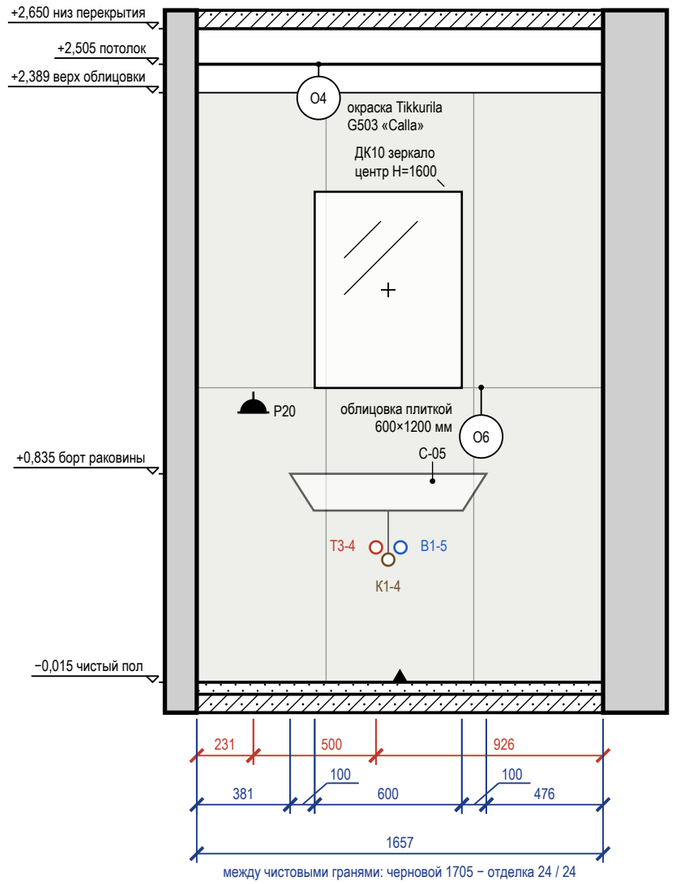

между чистовыми гранями: черновой 1705 − отделка 24 / 24

Стена Г — визуализация, лист 5




Ведомость отделки (на листе)

Марка	Поверхность	Материал, изделие	Цвет, код	Кол.
О4	потолок	окраска, Tikkurila Euro Power 7, матовая, подготовка Q3	Tikkurila G503 «Calla»	4 м²
О6	стены	облицовка плиткой, 600×1200×9 мм, аналог: керамогранит под травертин, матовый, затирка CG2WA		7,8 м²

Ведомость точек и выводов

Стена	Марка	Что это	Гр.	Н, мм	От угла, мм	Примечание
В	ТР1	терморегулятор: терморегулятор тёплого пола	19	1000	1916	
В	ЭВ8	вывод кабеля: вентилятор в потолке (знак 11 по исходному плану; вывод — в запотолочное пространство) ВР2 (клавиша L13, таймер выбега)	2	2400	2116	
В	КУП2	КУП (уравнивание потенциалов): КУП уравнивание потенциалов (ДСУП)		300	2166	
Г	Р20	розетка: фен у умывальника	15	1100	231	IP44
Г	Т3-4	горячая вода — умывальник		550	731	межос. 100
Г	К1-4	канализация — умывальник		500	781	Ø40
Г	В1-5	холодная вода — умывальник		550	831	межос. 100

Схема развёрток (М 1:50)

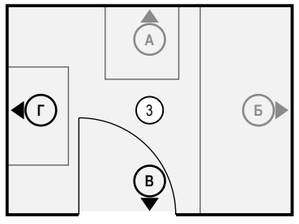

Ведомость изделий и проёмов (на листе)

Стена	Марка	Изделие, проём	На виде Ш×В, мм	Низ, мм
В	С-04	ванна 1700×750 акриловая, экран под плитку	726×600	0
В	Д-3	дверь	790×2100	0
Г	С-05	умывальник на тумбе 800: тумба подвесная, шпон ореха, столешница-раковина из литого мрамора	800×150	700
Г	ДК10	зеркало	600×800	1200

Примечания

1. Размеры — в мм от чистовых поверхностей стен; условные обозначения и общие указания — лист 12.
2. Облицовка — по сетке швов 2 мм, раскладка от оси стены (треугольник у пола), целые ряды от пола; подрезки — по листу раскладки плитки.
3. Гидроизоляция в 2 слоя, заход на стены 200 мм; над ванной — до 2000 и 300 мм за борт — до облицовки, с актом скрытых работ и тестом проливом (узел — на листе узлов).
4. Картины и зеркала крепить к основанию по паспорту изделия (закладные и анкеры — в перечне скрытых работ); крест — ось центра предмета.

	Лист	№ док.	Подпись	Дата
Дизайнер	Кырлан А.С.			13.11.26
Проверил				
Н. контр.				
Утв.				


Проект: Квартира 68 м², элитный модерн — **М 1:25**

Развёртки стен В, Г. Ванная (пом. 3)

Стадия	Лист	Листов
П	60	94


выпуск 13.11.2026 № c38d47cb31 · стр. 60 из 94

Стена А (М 1:25)

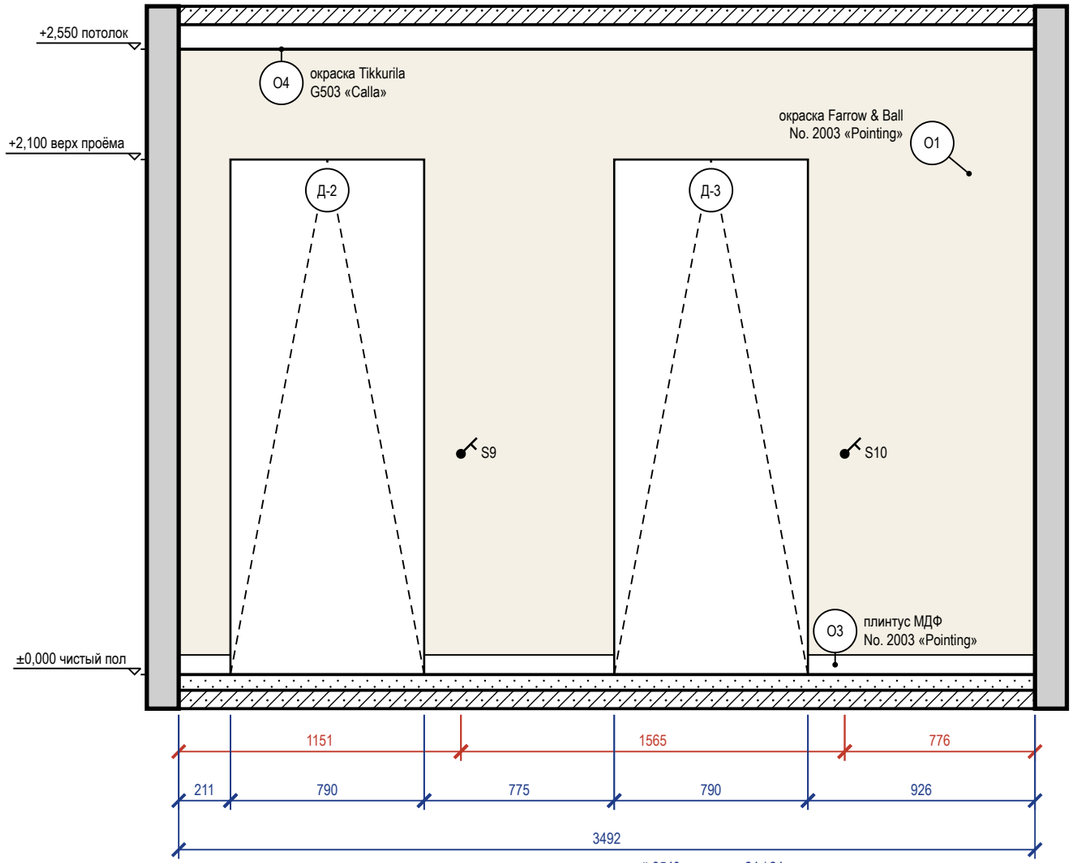

между чистовыми гранями: черновой 3540 − отделка 24 / 24

Стена Б (М 1:25)

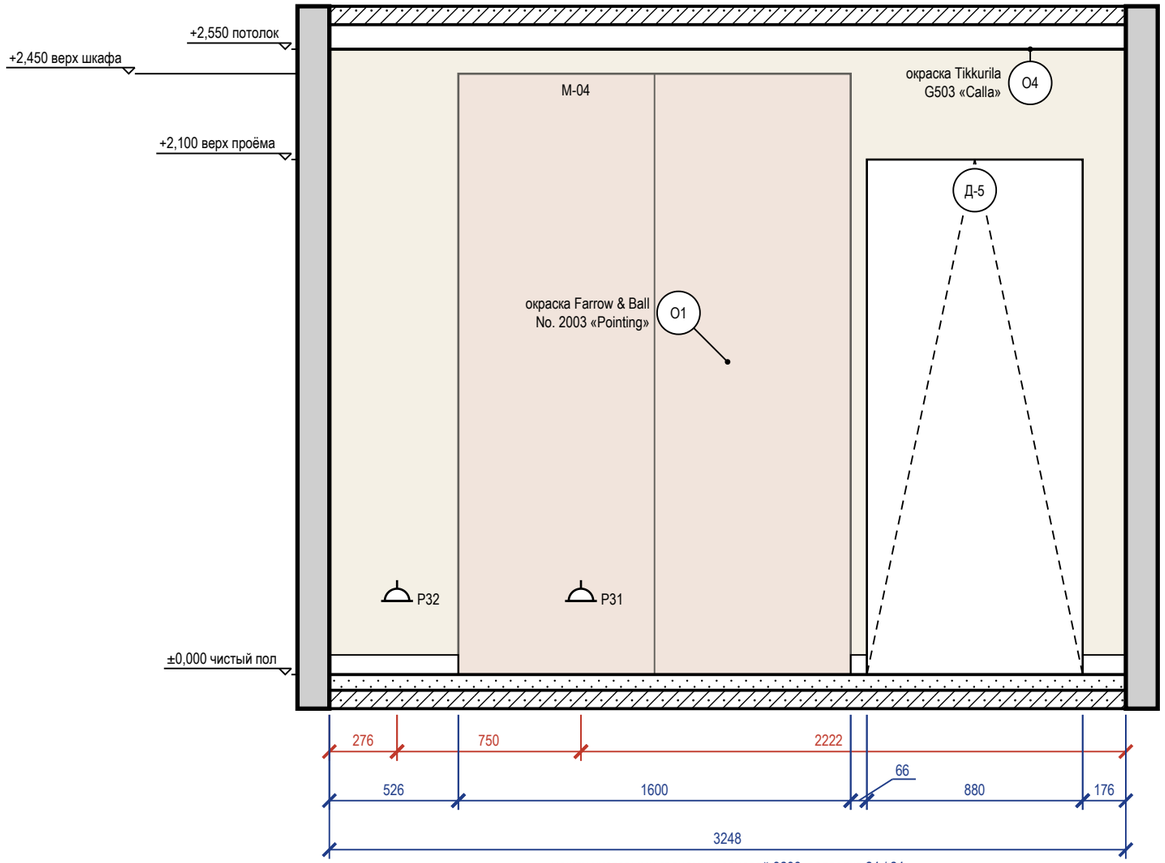


между чистовыми гранями: черновой 3296 − отделка 24 / 24

Ведомость точек и выводов

Стена	Марка	Что это	Гр.	Н, мм	От угла, мм	Примечание
А	S9	выключатель: свет санузел (у двери)	2	900	1151	
А	S10	выключатель: свет ванная (у двери)	2	900	2716	
Б	Р32	розетка: док-станция робота-пылесоса	16	300	276	
Б	Р31	розетка: у обувной полки (сушка обуви)	16	300	1026	

Схема развёрток (М 1:200)

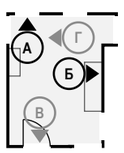

Стена Б — визуализация, лист 8



Ведомость отделки (на листе)

Марка	Поверхность	Материал, изделие	Цвет, код	Кол.
О1	стены	окраска, Farrow & Ball Modern Emulsion, матовая, подготовка Q3	Farrow & Ball No. 2003 «Pointing»	7,9 м²
О3	плинтус	плинтус МДФ, h 80 мм, аналог: плинтус МДФ под покраску 80×16	Farrow & Ball No. 2003 «Pointing»	2,7 м
О4	потолок	окраска, Tikkurila Euro Power 7, глубокоматовая, подготовка Q3	Tikkurila G503 «Calla»	13,9 м²

Примечания

1. Размеры — в мм от чистовых поверхностей стен; условные обозначения и общие указания — лист 12.
2. Потолок — у каждой стены свой, по плану потолков (ПТ3); ступени — зоной, кромка короба перед нишей — тонкой линией; в поле потолка: ПТ4 +2,650.

	Лист	№ док.	Подпись	Дата
Дизайнер	Кырлан А.С.			13.11.26
Проверил				
Н. контр.				
Утв.				


Проект: Квартира 68 м², элитный модерн — М 1:25

Развёртки стен А, Б. Прихожая (пом. 4)

Стадия	Лист	Листов
П	61	94


выпуск 13.11.2026 № c38d47cb31 · стр. 61 из 94

Стена В (М 1:25)

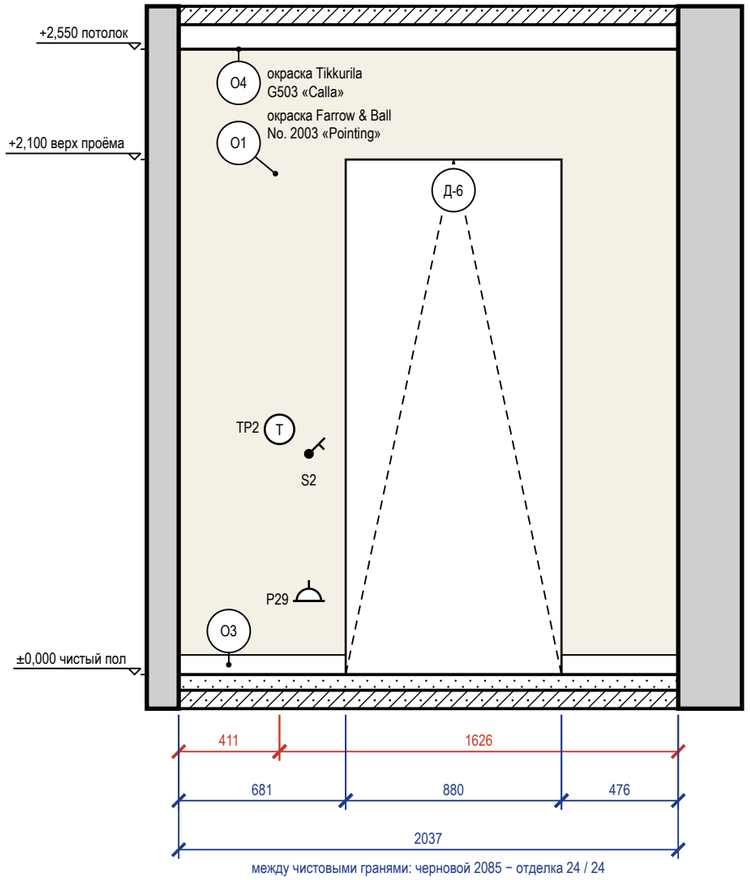

между чистовыми гранями: черновой 2085 − отделка 24 / 24

Стена Г (М 1:25)

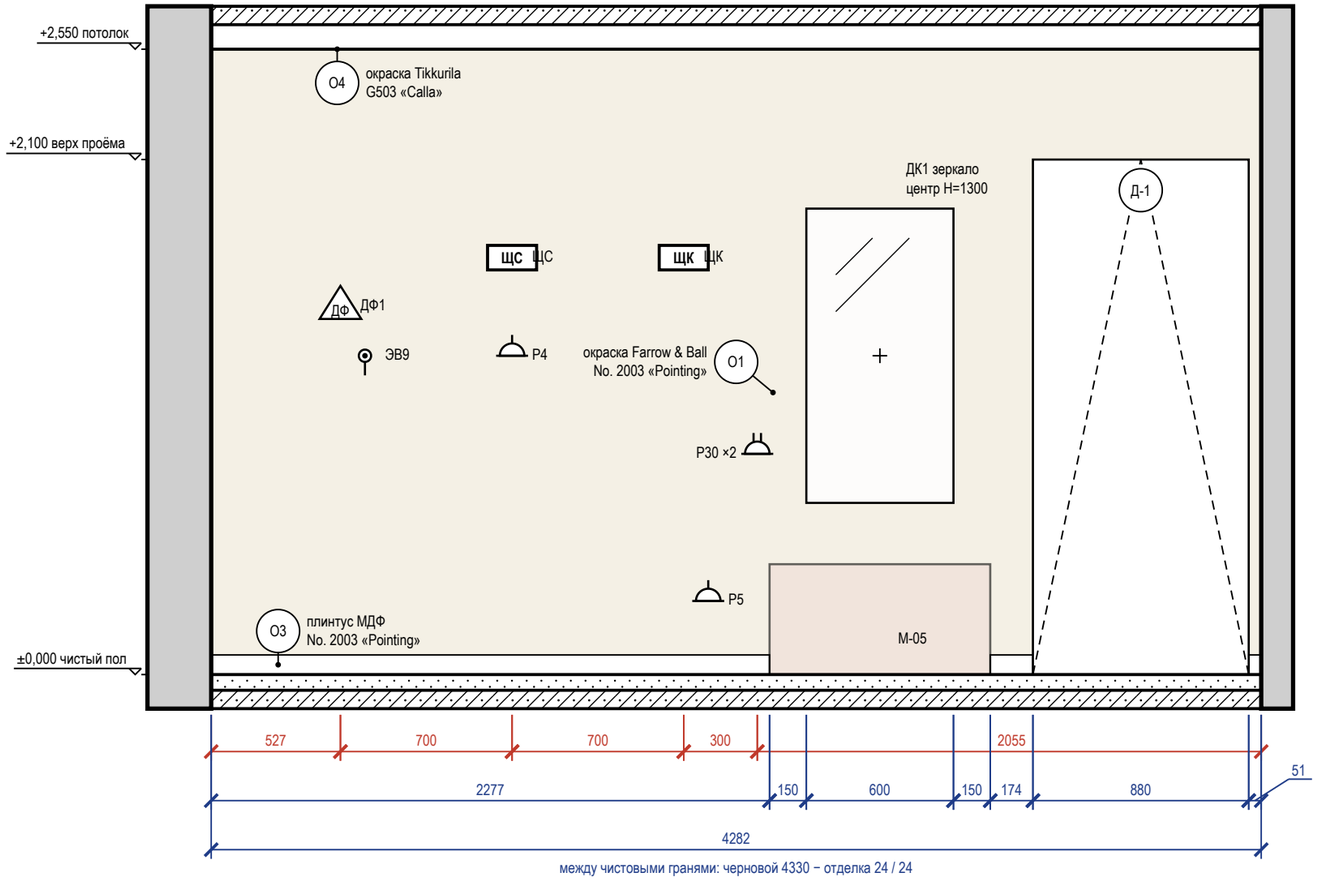

между чистовыми гранями: черновой 4330 − отделка 24 / 24


Ведомость точек и выводов

Стена	Марка	Что это	Гр.	H, мм	От угла, мм	Примечание
В	TP2	терморегулятор: терморегулятор тёплого пола	19	1000	411	
В	P29	розетка: уборка у входа	16	300	531	
В	S2	выключатель	1	900	531	
Г	ДФ1	домофон: трубка домофона		1500	527	
Г	ЭВ9	вывод кабеля: контроллер защиты от протечек и питание электрокранов (у слаботочного щита)	16	1300	627	
Г	P4	розетка: питание слаботочного щита (роутер, ONT)	16	1300	1227	
Г	ЩС	щит: щит слаботочный: ввод провайдера, ONT, роутер		1700	1227	
Г	ЩК	щит: щит квартирный ЩРВ-П-72, IP41		1700	1927	
Г	P5	розетка: уборка, сушилка обуви	7	300	2027	
Г	P30	розетка: прихожая: зарядка телефона и ключей	16	900	2227	рамка 2 поста

Ведомость отделки (на листе)

Марка	Поверхность	Материал, изделие	Цвет, код	Кол.
O1	стены	окраска, Farrow & Ball Modern Emulsion, матовая, подготовка Q3	Farrow & Ball No. 2003 «Pointing»	12,4 м²
O3	плинтус	плинтус МДФ, h 80 мм, аналог: плинтус МДФ под покраску 80×16	Farrow & Ball No. 2003 «Pointing»	3,7 м
O4	потолок	окраска, Tikkurila Euro Power 7, глубокоматовая, подготовка Q3	Tikkurila G503 «Calla»	13,9 м²

Схема развёрток (М 1:100)

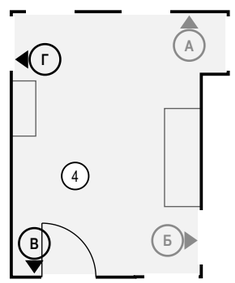


Примечания

1. Размеры — в мм от чистовых поверхностей стен; условные обозначения и общие указания — лист 12.
2. Картины и зеркала крепить к основанию по паспорту изделия (закладные и анкеры — в перечне скрытых работ); крест — ось центра предмета.
3. Потолок — у каждой стены свой, по плану потолков (ПТ3); ступени — зоной, кромка короба перед нишей — тонкой линией; в поле потолка: ПТ4 +2,650.

	Лист	№ док.	Подпись	Дата	Проект: Квартира 68 м², элитный модерн			М 1:25
Дизайнер	Кырлан А.С.			13.11.26	Развёртки стен В, Г. Прихожая (пом. 4)	Стадия	Лист	Листов
Проверил						П	62	94
Н. контр.								
Утв.								


Стена А1 (М 1:20)

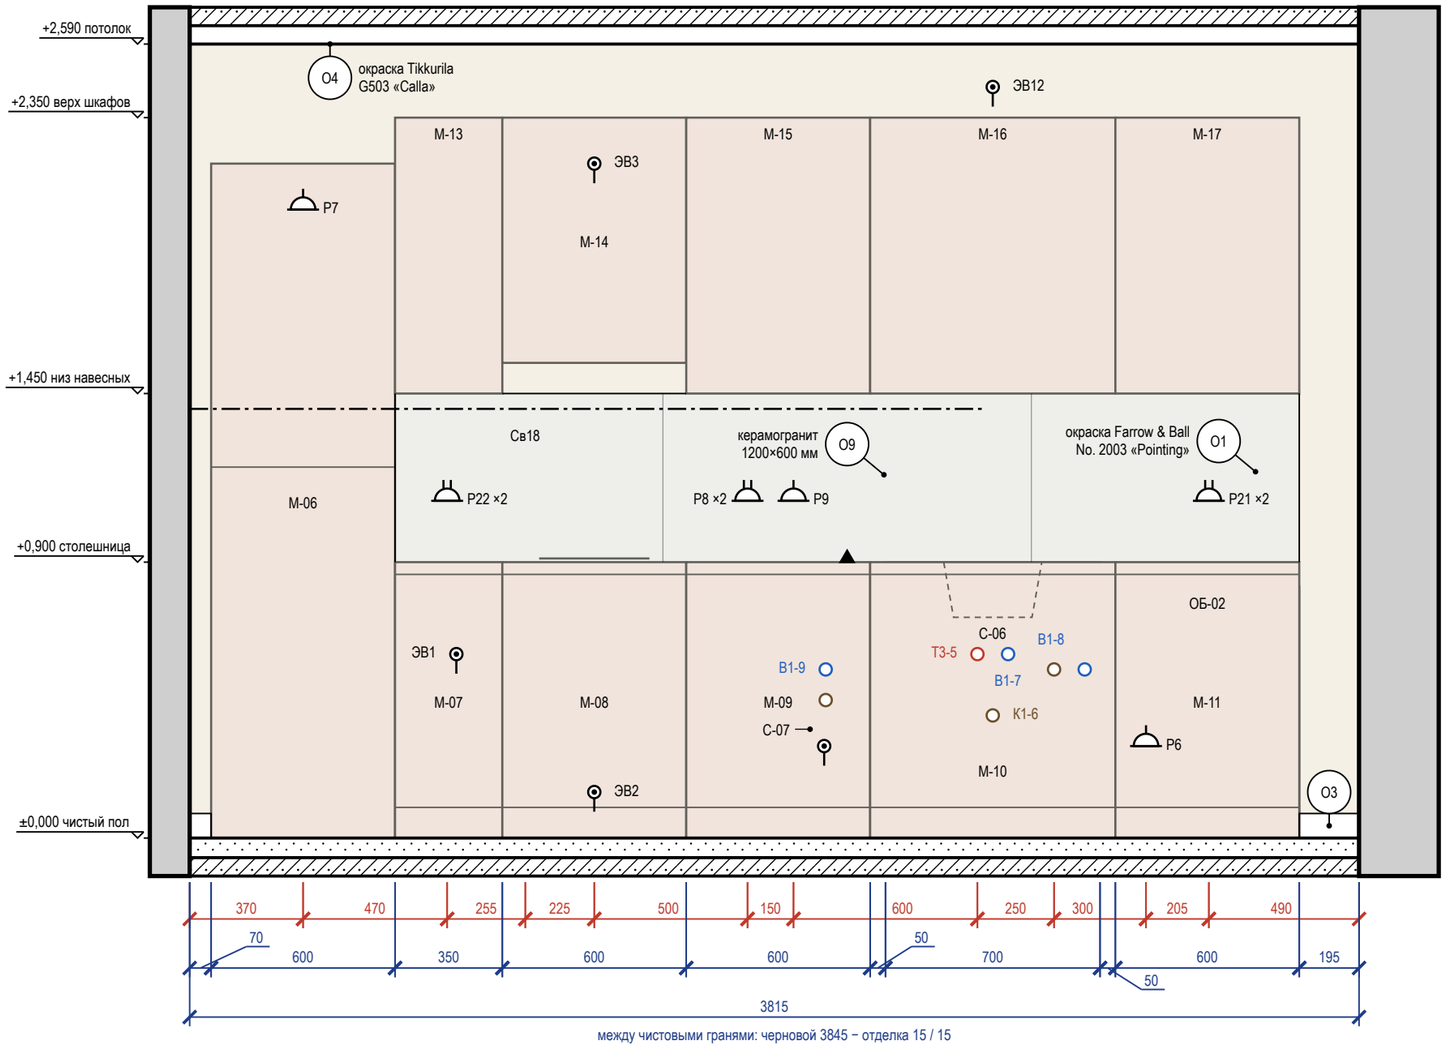

Ведомость точек и выводов

Марка	Что это	Гр.	Н, мм	От угла, мм	Примечание
Р7	розетка: холодильник — над нишей, съёмная панель	10	2050	370	
Р22	розетка: фартук	8	1100	840	рамка 2 поста
ЭВ1	вывод кабеля: варочная панель — в соседнем модуле, за ящиком	12	600	870	
Св18	светильник настенный: марка 13 по исходному плану: «підсвітка робочої поверхні»	1	1400	1095	лента -405–2595 от угла
ЭВ2	вывод кабеля: духовой шкаф — в цоколе	13	150	1320	
ЭВ3	вывод кабеля: вытяжка — над корпусом	11	2200	1320	
Р8	розетка: чайник и кофемашина (отдельная линия)	9	1100	1820	рамка 2 поста
Р9	розетка: фартук: мелкая техника	8	1100	1970	
ЭВ11	вывод кабеля: измельчитель мойки	8	300	2070	
К1-8	канализация — фильтр обратного осмоса		450	2075	Ø40
В1-9	холодная вода — фильтр обратного осмоса		550	2075	
Т3-5	горячая вода — мойка кухонная		600	2570	межос. 100
К1-6	канализация — мойка кухонная		400	2620	Ø50
ЭВ12	вывод кабеля: подсветка навесных шкафов (блок питания ленты)	8	2450	2620	
В1-7	холодная вода — мойка кухонная		600	2670	межос. 100
К1-7	канализация — посудомоечная машина		550	2820	Ø40; слив ПММ в шкафу мойки
В1-8	холодная вода — посудомоечная машина		550	2920	кран ПММ в шкафу мойки
Р6	розетка: посудомоечная машина (в нише М-11, сбоку от корпуса, доступ через цоколь)	14	300	3120	
Р21	розетка: фартук	8	1100	3325	рамка 2 поста

Схема развёрток (М 1:50)

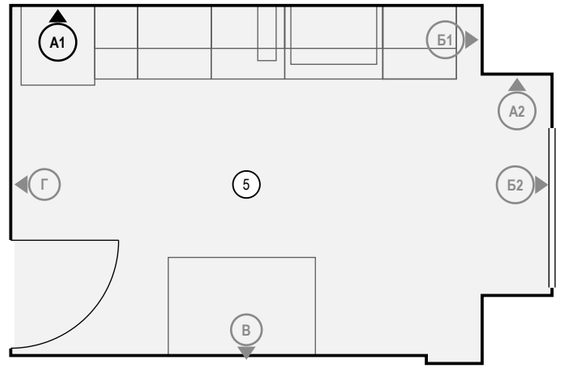

Ведомость отделки (на листе)

Марка	Поверхность	Материал, изделие	Цвет, код	Кол.
О1	стены	окраска, Farrow & Ball Modern Emulsion, матовая, подготовка Q3	Farrow & Ball No. 2003 «Pointing»	8,3 м²
О3	плинтус	плинтус МДФ, h 80 мм, аналог: плинтус МДФ под покраску 80×16	Farrow & Ball No. 2003 «Pointing»	0,3 м
О4	потолок	окраска, Tikkurila Euro Power 7, глубокоматовая, подготовка Q3	Tikkurila G503 «Calla»	12 м²
О9	фартук	керамогранит, 1200×600×9 мм, аналог: керамогранит под травертин, матовый, затирка CG2WA		1,6 м²


Примечания

1. Размеры — в мм от чистовых поверхностей стен; условные обозначения и общие указания — лист 12.
2. Схема мебели, приборов и декора не является технической документацией для производства мебели; габариты — по паспортам изделий.
3. Выводы кухонной техники — по утверждённому проекту кухни: привязки выводов даются от осей модулей гарнитура.
4. Часть марок не уместилась у знаков: коды, высоты и привязки этих позиций — в ведомости точек и выводов под видами.

	Лист	№ док.	Подпись	Дата	Проект: Квартира 68 м², элитный модерн		М 1:20
Дизайнер	Кырлан А.С.			13.11.26	Развёртка стены А1. Кухня-столовая (пом. 5), кухонный фронт	Стадия	Лист	Листов
Проверил						П	63	94
Н. контр.								
Утв.								


выпуск 13.11.2026 № c38d47cb31 · стр. 63 из 94

Стена А2 (М 1:20)

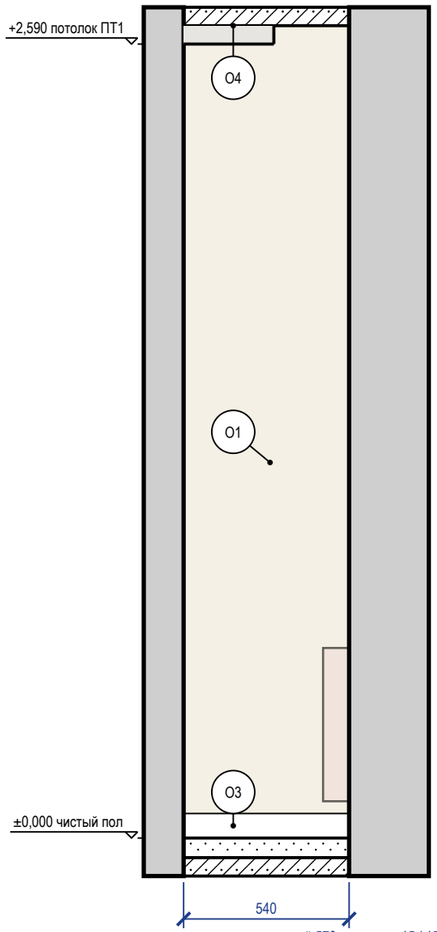


между чистовыми гранями: черновой 570 − отделка 15 / 15

Стена Б1 (М 1:20)

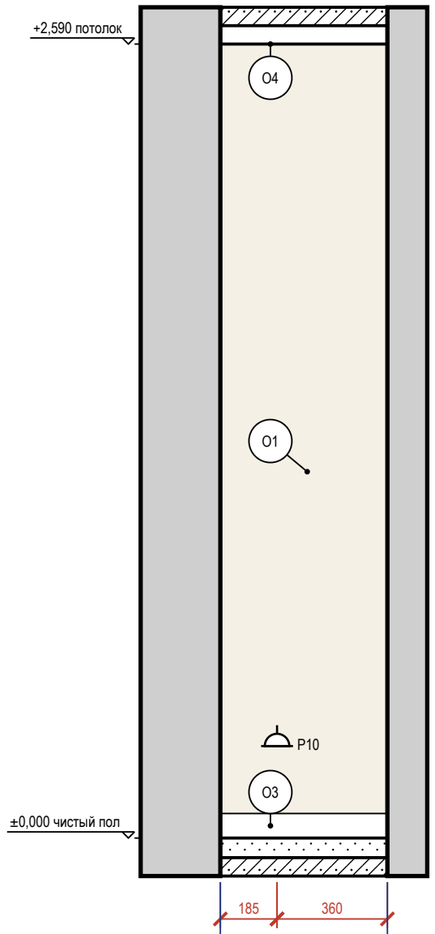

между чистовыми гранями: черновой 560 − отделка 15 / 0

Стена Б2 (М 1:20)

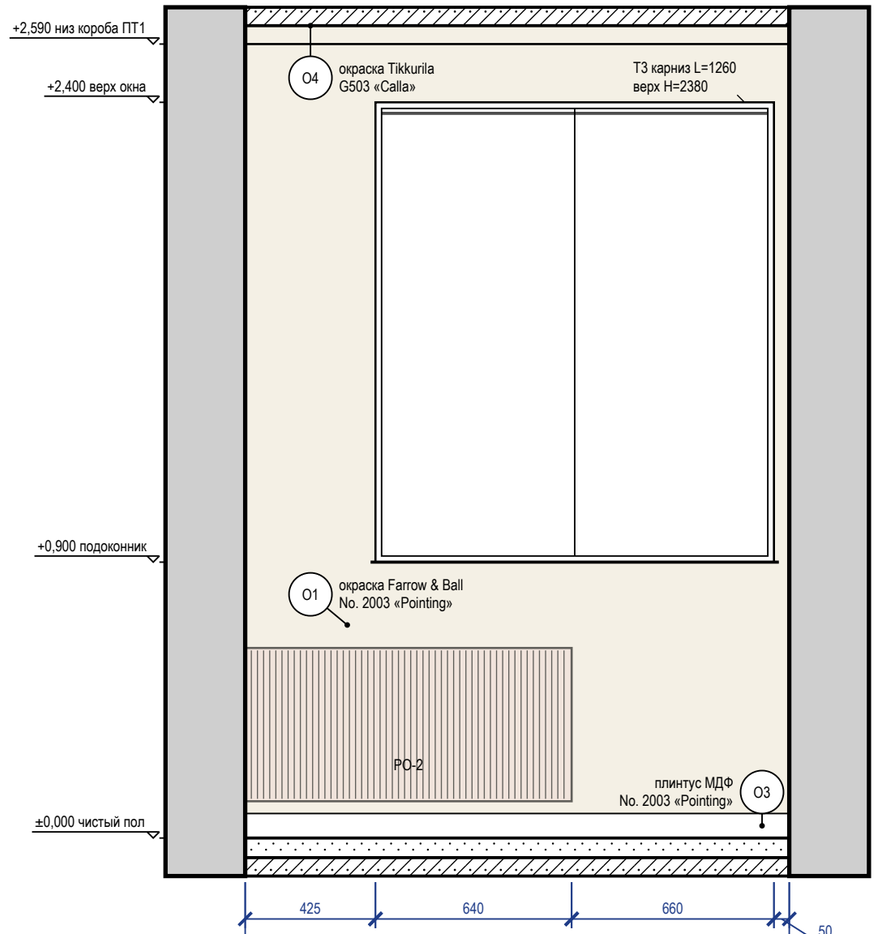

между чистовыми гранями: черновой 1805 − отделка 15 / 15

Ведомость точек и выводов

Стена	Марка	Что это	Гр.	Н, мм	От угла, мм	Примечание
Б1	Р10	розетка: общего назначения	4	300	185	


Ведомость изделий и проёмов (на листе)

Стена	Марка	Изделие, проём	На виде Ш×В, мм	Низ, мм
А2	РО-2	радиатор отопления	85×500	120
Б2	РО-2	радиатор отопления	1065×500	120

Ведомость отделки (на листе)

Марка	Поверхность	Материал, изделие	Цвет, код	Кол.
О1	стены	окраска, Farrow & Ball Modern Emulsion, матовая, подготовка Q3	Farrow & Ball No. 2003 «Pointing»	5,6 м²
О3	плинтус	плинтус МДФ, h 80 мм, аналог: плинтус МДФ под покраску 80×16	Farrow & Ball No. 2003 «Pointing»	2,9 м
О4	потолок	окраска, Tikkurila Euro Power 7, глубокоматовая, подготовка Q3	Tikkurila G503 «Calla»	12 м²

Схема развёрток (М 1:100)

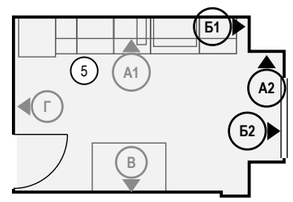

Примечания

1. Размеры — в мм от чистовых поверхностей стен; условные обозначения и общие указания — лист 12.
2. Карнизы (шины) — по ведомости текстиля декоратора: длина L и верх H на развёртке — те же числа, что в ведомости; крепление — до окраски потолка.

	Лист	№ док.	Подпись	Дата
Дизайнер	Кырлан А.С.			13.11.26
Проверил				
Н. контр.				
Утв.				


Проект: Квартира 68 м², элитный модерн — **М 1:20**

Развёртки стен А2, Б1, Б2. Кухня-столовая (пом. 5)


Стадия	Лист	Листов
П	64	94

выпуск 13.11.2026 № c38d47cb31 · стр. 64 из 94

Стена В (М 1:25)

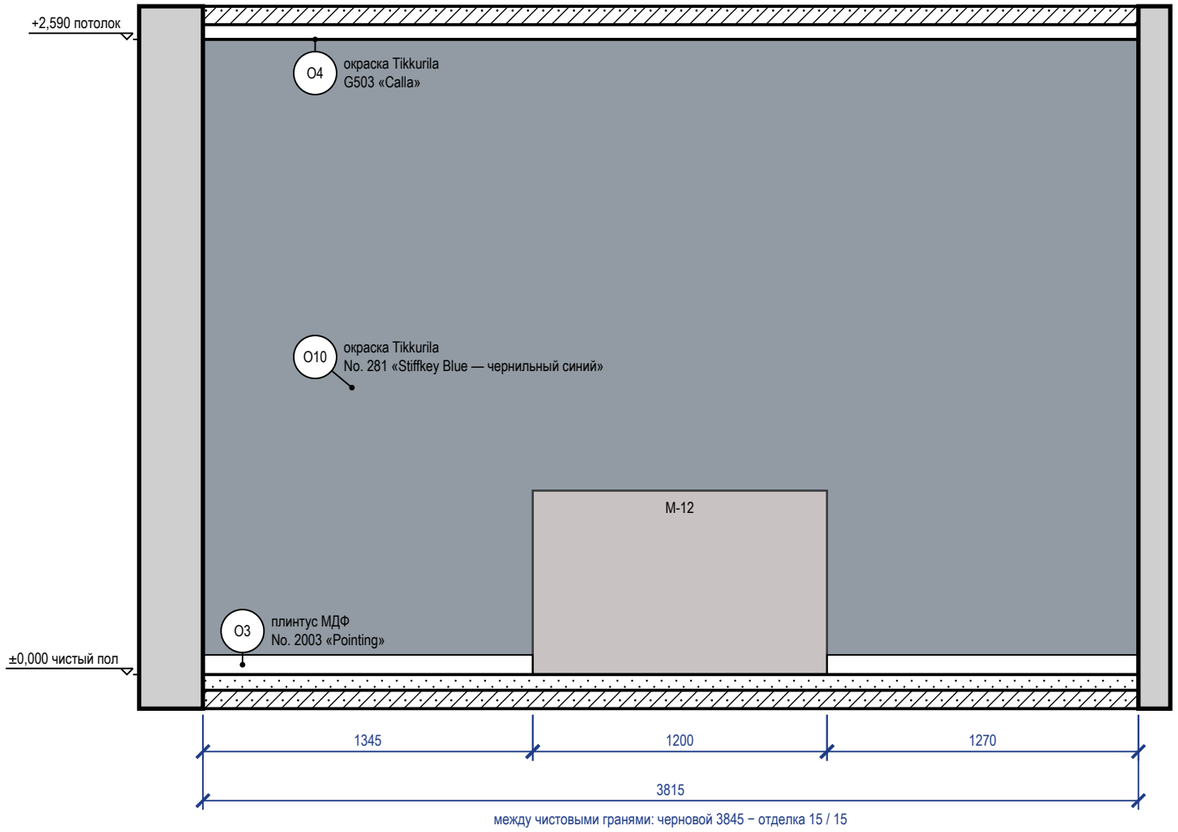

Стена Г (М 1:25)

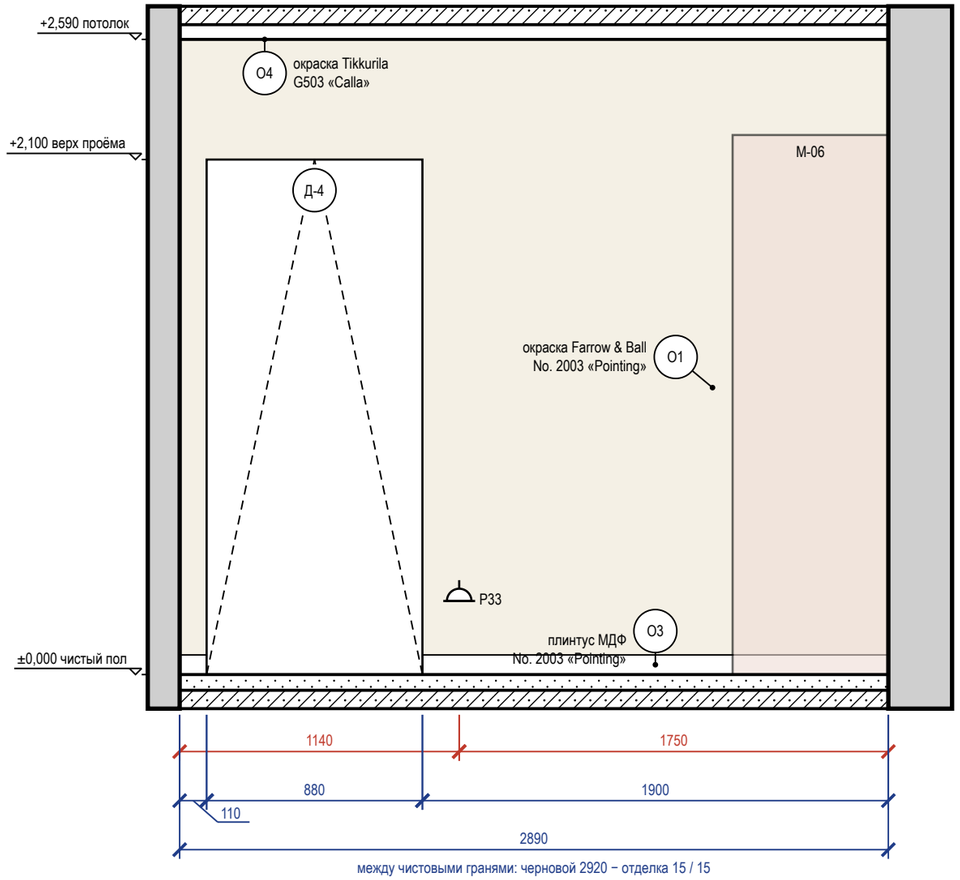

Ведомость точек и выводов

Стена	Марка	Что это	Гр.	Н, мм	От угла, мм	Примечание
Г	Р33	розетка: уборка у входа	8	300	1140	


Ведомость изделий и проёмов (на листе)

Стена	Марка	Изделие, проём	На виде Ш×В, мм	Низ, мм
В	М-12	стол обеденный 1200×800, мраморная столешница, опора латунь; стулья с мягкой спинкой, 4 шт.	1200×750	0
Г	Д-4	дверь	880×2100	0
Г	М-06	колонна с холодильником встроенным; фасады — МДФ: шпон американского ореха (нижние модули) и эмаль пыльно-синяя с узкой филёнкой (колонны), латунные ручки-скобы; фурнитура — латунь брашированная	635×2200	0

Ведомость отделки (на листе)

Марка	Поверхность	Материал, изделие	Цвет, код	Кол.
О1	стены	окраска, Farrow & Ball Modern Emulsion, матовая, подготовка Q3	Farrow & Ball No. 2003 «Pointing»	5,6 м²
О3	плинтус	плинтус МДФ, h 80 мм, аналог: плинтус МДФ под покраску 80×16	Farrow & Ball No. 2003 «Pointing»	4,6 м
О4	потолок	окраска, Tikkurila Euro Power 7, глубокоматовая, подготовка Q3	Tikkurila G503 «Calla»	12 м²
О10	акцентная стена	окраска, Tikkurila Euro Power 7, колеровка по NCS, матовая, подготовка Q3	Farrow & Ball No. 281 «Stiffkey Blue — чернильный синий»	9,9 м²

Схема развёрток (М 1:50)

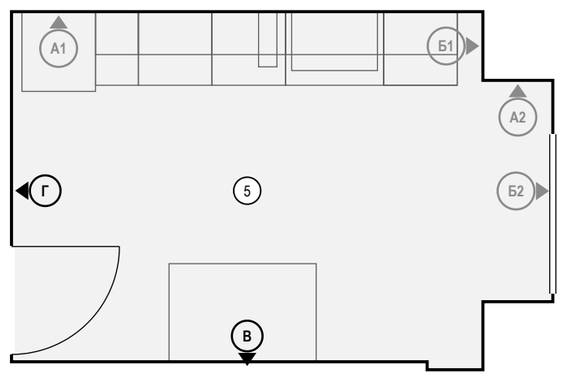


Примечания

1. Размеры — в мм от чистовых поверхностей стен; условные обозначения и общие указания — лист 12.

	Лист	№ док.	Подпись	Дата	Проект: Квартира 68 м², элитный модерн	М 1:25		
Дизайнер	Кырлан А.С.			13.11.26	Развёртки стен В, Г. Кухня-столовая (пом. 5)	Стадия	Лист	Листов
Проверил						П	65	94
Н. контр.								
Утв.								


выпуск 13.11.2026 № c38d47cb31 · стр. 65 из 94

Стена А (М 1:25)

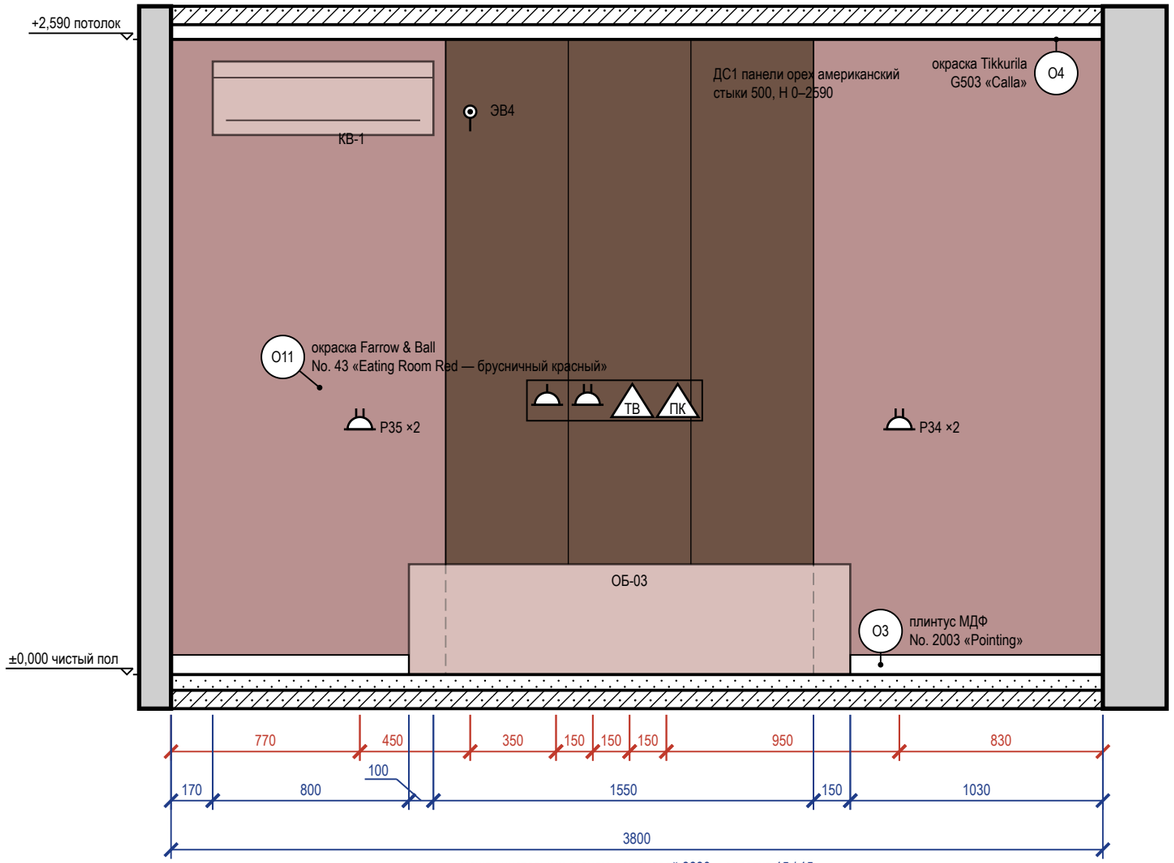

между чистовыми гранями: черновой 3830 − отделка 15 / 15

Стена Б (М 1:25)

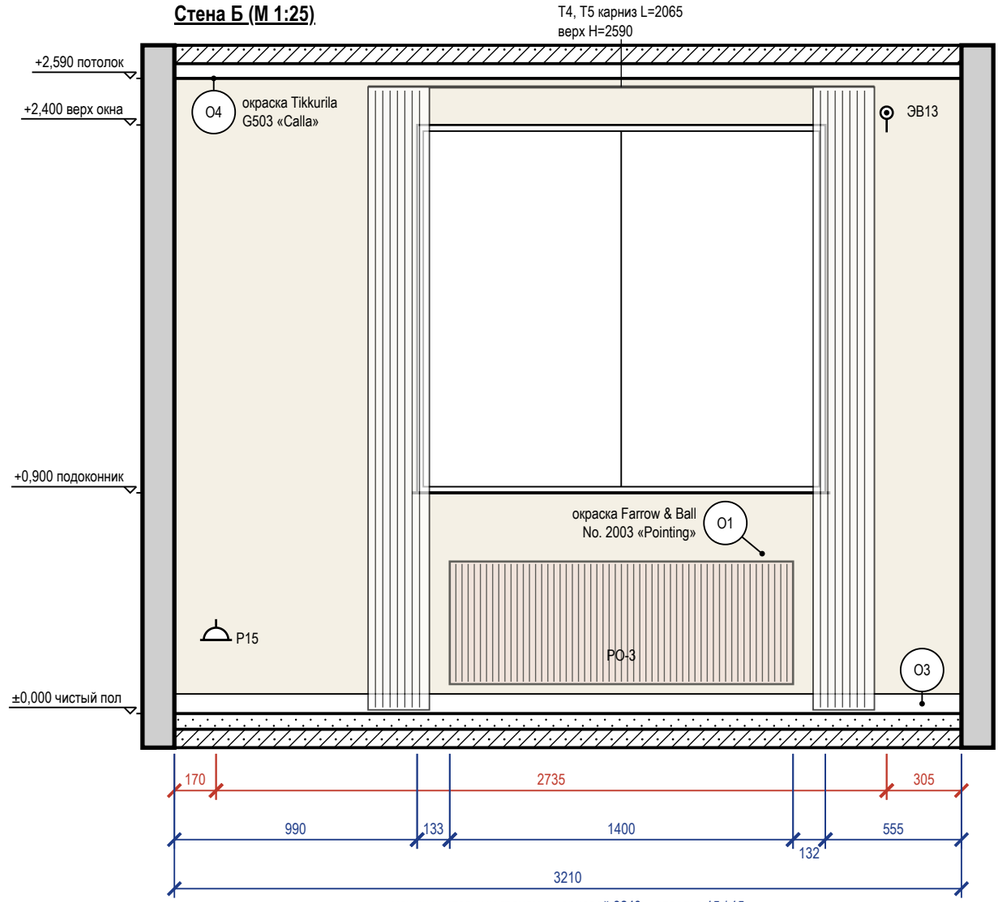

между чистовыми гранями: черновой 3240 − отделка 15 / 15

Ведомость точек и выводов

Стена	Марка	Что это	Гр.	Н, мм	От угла, мм	Примечание
А	Р35	розетка: ТВ-зона: приставка, консоль, саундбар	5	1000	770	рамка 2 поста
А	ЭВ4	вывод кабеля: кондиционер КВ-1 — вывод питания внутреннего блока	17	2295	1220	
А	Р12	розетка: саундбар	5	1100	1570	
А	Р11	розетка: ТВ, приставка	5	1100	1720	рамка 2 поста
А	ТВ1	розетка ТВ: ТВ-зона		1100	1870	
А	LAN2	розетка RJ45: Smart TV		1100	2020	
А	Р34	розетка: ТВ-зона: приставка, консоль, саундбар	5	1000	2970	рамка 2 поста
Б	Р15	розетка: уборка	5	300	170	
Б	ЭВ13	вывод кабеля: электрокарниз (привод штор)	5	2450	2905	

Стена Б — визуализация, лист 10


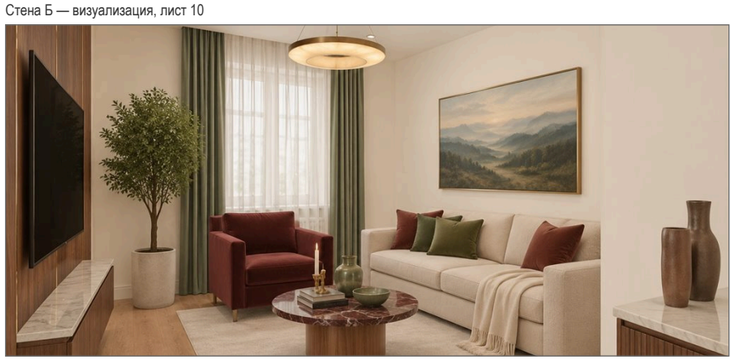


Схема развёрток (М 1:100)

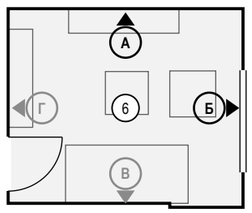


Примечания

1. Размеры — в мм от чистовых поверхностей стен; условные обозначения и общие указания — лист 12.
2. Отделка стен — по ведомости отделки помещений, лист С1.
3. Объёмная отделка стен — по ведомости отделки листа: материал, сечение, шаг и отметки — по подписи у элемента; рейки и рамки молдингов раскладываются от середины поля; крепление — по паспорту изделия.
4. Объёмная отделка за мебелью и приборами не показана, граница её поля за ними — штриховой линией.
5. Карнизы (шины) — по ведомости текстиля декоратора: длина L и верх Н на развёртке — те же числа, что в ведомости; крепление — до окраски потолка.
6. Часть марок не уместилась у знаков: коды, высоты и привязки этих позиций — в ведомости точек и выводов под видами.


	Лист	№ док.	Подпись	Дата	Проект: Квартира 68 м², элитный модерн			М 1:25
Дизайнер	Кырлан А.С.			13.11.26	Развёртки стен А, Б. Гостиная (пом. 6)	Стадия	Лист	Листов
Проверил						П	66	94
Н. контр.								
Утв.								

Стена В (М 1:25)

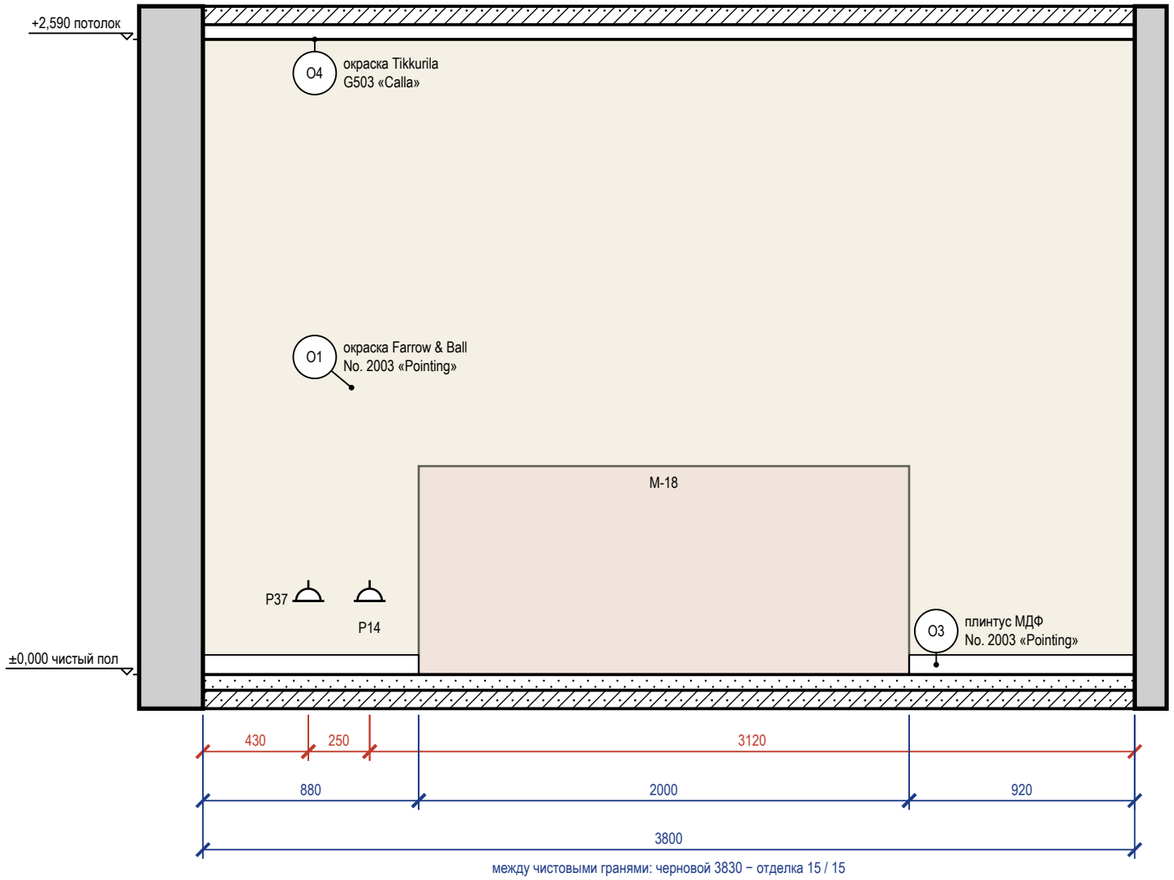

между чистовыми гранями: черновой 3830 − отделка 15 / 15

Стена Г (М 1:25)

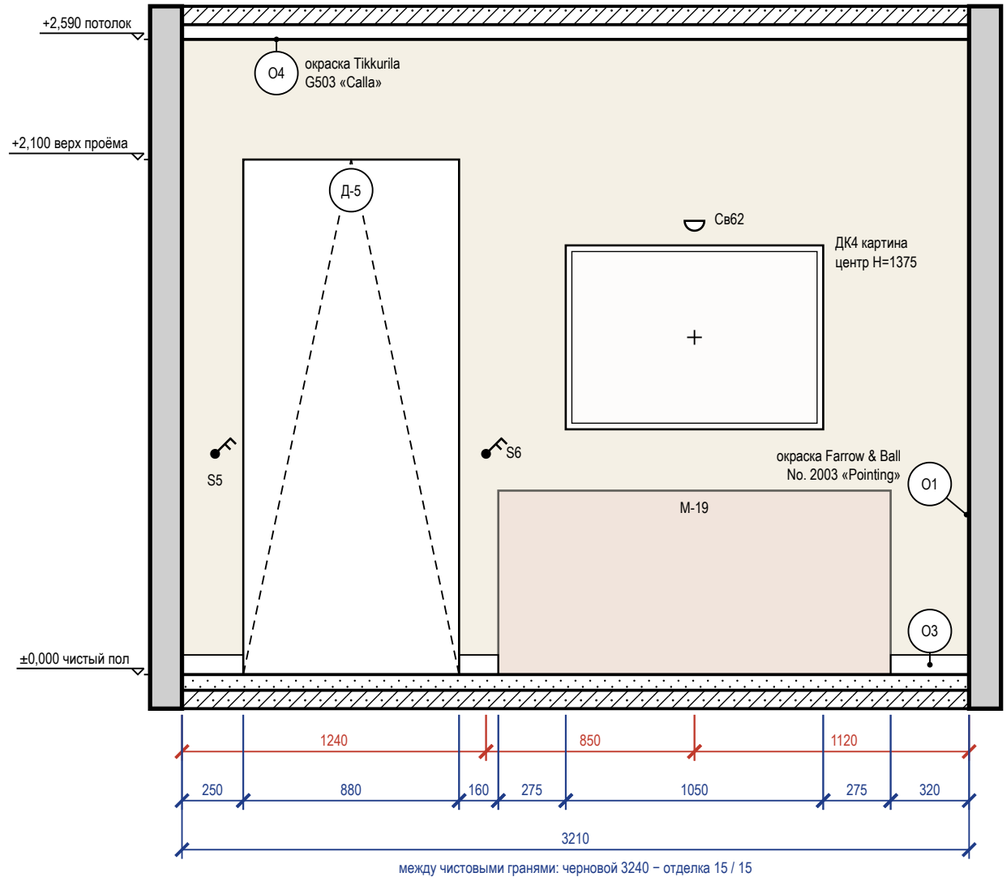


между чистовыми гранями: черновой 3240 − отделка 15 / 15


Ведомость точек и выводов

Стена	Марка	Что это	Гр.	H, мм	От угла, мм	Примечание
В	Р37	розетка: у дивана: торшер, зарядка	5	300	430	
В	Р14	розетка: у дивана: зарядка	5	300	680	
Г	S5	выключатель	1	900	135	
Г	S6	выключатель	1	900	1240	
Г	Св62	светильник настенный	1	1850	2090	

Схема развёрток (М 1:200)

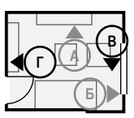

Стена В — визуализация, лист 9

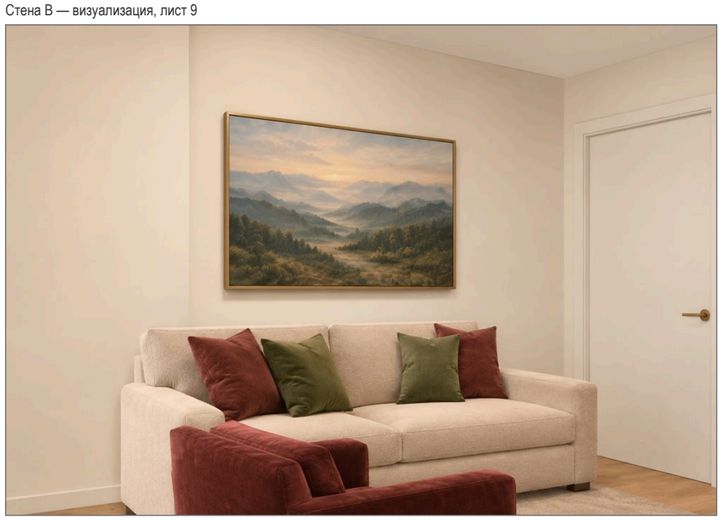

Ведомость отделки (на листе)

Марка	Поверхность	Материал, изделие	Цвет, код	Кол.
О1	стены	окраска, Farrow & Ball Modern Emulsion, матовая, подготовка Q3	Farrow & Ball No. 2003 «Pointing»	16,3 м²
О3	плинтус	плинтус МДФ, h 80 мм, аналог: плинтус МДФ под покраску 80×16	Farrow & Ball No. 2003 «Pointing»	2,5 м
О4	потолок	окраска, Tikkurila Euro Power 7, глубокоматовая, подготовка Q3	Tikkurila G503 «Calla»	12,2 м²


Примечания

1. Размеры — в мм от чистовых поверхностей стен; условные обозначения и общие указания — лист 12.
2. Картины и зеркала крепить к основанию по паспорту изделия (закладные и анкеры — в перечне скрытых работ); крест — ось центра предмета.

	Лист	№ док.	Подпись	Дата	Проект: Квартира 68 м², элитный модерн			М 1:25
Дизайнер	Кырлан А.С.			13.11.26	Развёртки стен В, Г. Гостиная (пом. 6)	Стадия	Лист	Листов
Проверил						П	67	94
Н. контр.								
Утв.								


выпуск 13.11.2026 № c38d47cb31 · стр. 67 из 94

Стена А1 (М 1:20)

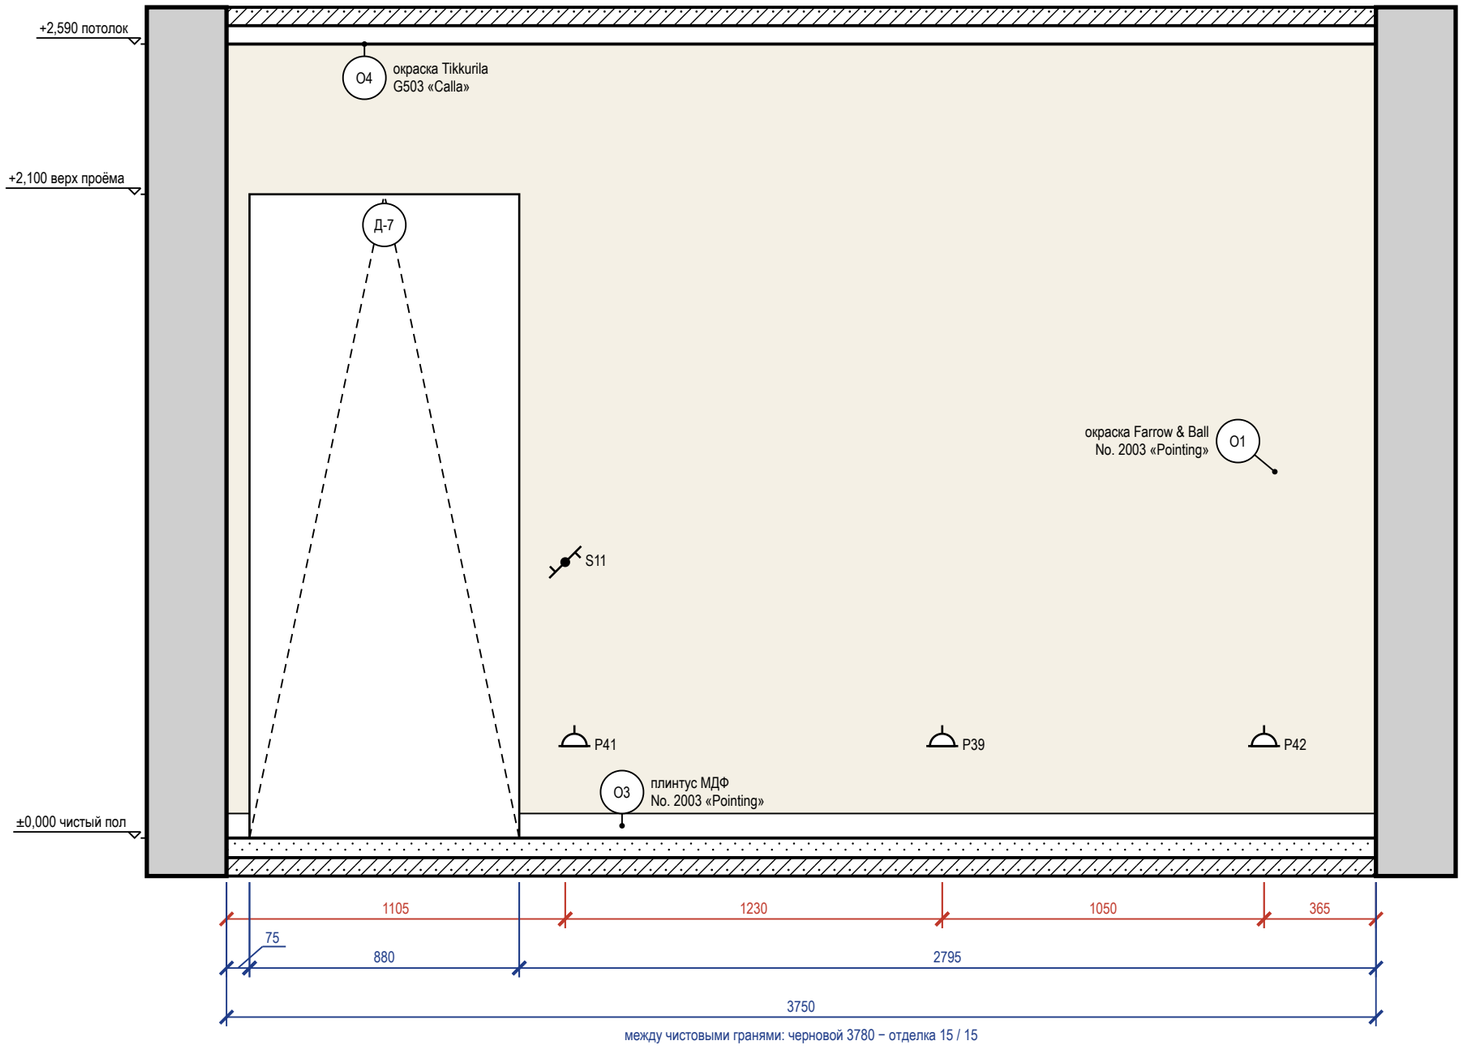

между чистовыми гранями: черновой 3780 − отделка 15 / 15

Схема развёрток (М 1:50)

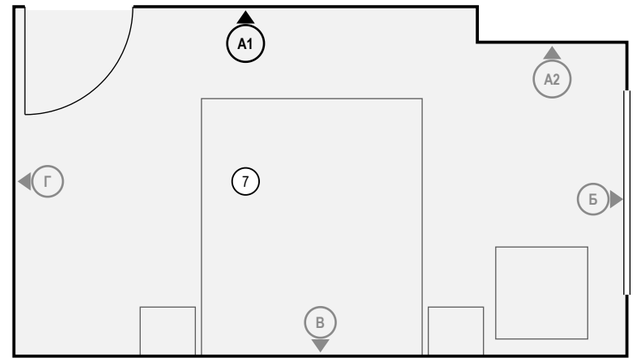

Ведомость точек и выводов

Марка	Что это	Гр.	Н, мм	От угла, мм	Примечание
S11	выключатель: основной свет спальни у входа (Д-7)	1	900	1105	
Р41	розетка: общего назначения	6	300	1135	
Р39	розетка: общего назначения	6	300	2335	
Р42	розетка: общего назначения	6	300	3385	

Ведомость отделки (на листе)

Марка	Поверхность	Материал, изделие	Цвет, код	Кол.
О1	стены	окраска, Farrow & Ball Modern Emulsion, матовая, подготовка Q3	Farrow & Ball No. 2003 «Pointing»	7,9 м²
О3	плинтус	плинтус МДФ, h 80 мм, аналог: плинтус МДФ под покраску 80×16	Farrow & Ball No. 2003 «Pointing»	2,9 м
О4	потолок	окраска, Tikkurila Euro Power 7, глубокоматовая, подготовка Q3	Tikkurila G503 «Calla»	13,9 м²

Ведомость изделий и проёмов (на листе)


Марка	Изделие, проём	На виде Ш×В, мм	Низ, мм
Д-7	дверь	880×2100	0

Примечания


1. Размеры — в мм от чистовых поверхностей стен; условные обозначения и общие указания — лист 12.

	Лист	№ док.	Подпись	Дата	Проект: Квартира 68 м², элитный модерн	М 1:20		
Дизайнер	Кырлан А.С.			13.11.26	Развёртка стены А1. Спальня (пом. 7)	Стадия	Лист	Листов
Проверил						П	68	94
Н. контр.								
Утв.								

Стена А2 (М 1:20)

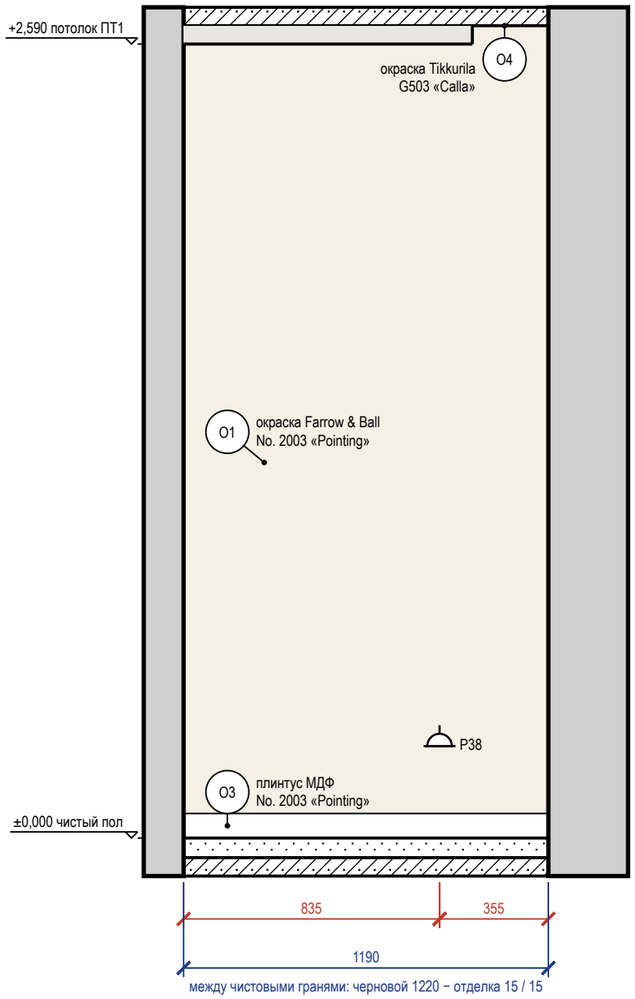

Стена Б (М 1:20)

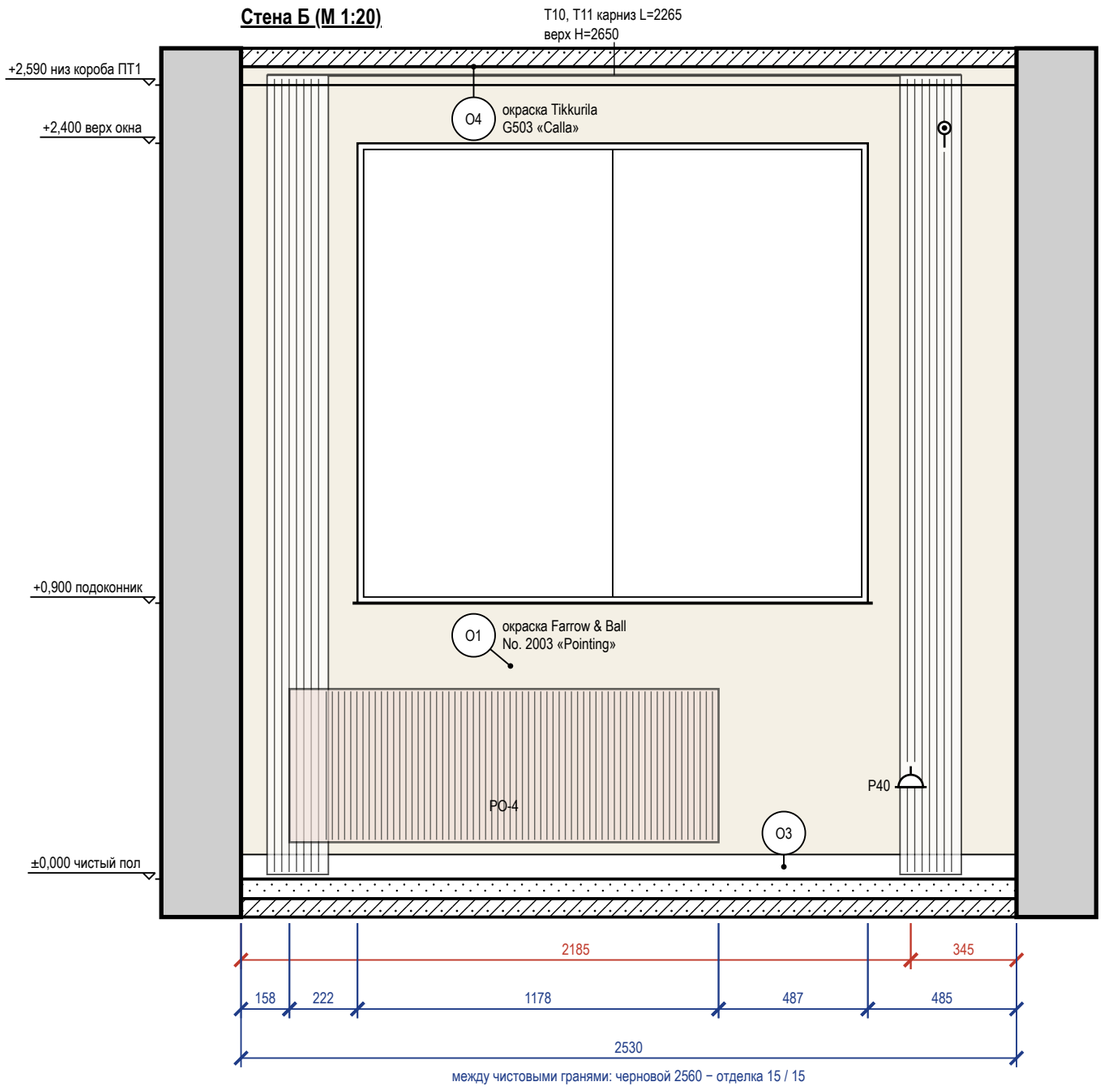

Ведомость точек и выводов

Стена	Марка	Что это	Гр.	H, мм	От угла, мм	Примечание
А2	Р38	розетка: общего назначения	6	300	835	
Б	Р40	розетка: общего назначения	6	300	2185	
Б	ЭВ14	вывод кабеля: электрокарниз (привод штор)	6	2450	2295	


Ведомость изделий и проёмов (на листе)

Стена	Марка	Изделие, проём	На виде Ш×В, мм	Низ, мм
Б	РО-4	радиатор отопления	1400×500	120

Ведомость отделки (на листе)

Марка	Поверхность	Материал, изделие	Цвет, код	Кол.
О1	стены	окраска, Farrow & Ball Modern Emulsion, матовая, подготовка Q3	Farrow & Ball No. 2003 «Pointing»	7,4 м²
О3	плинтус	плинтус МДФ, h 80 мм, аналог: плинтус МДФ под покраску 80×16	Farrow & Ball No. 2003 «Pointing»	3,7 м
О4	потолок	окраска, Tikkurila Euro Power 7, глубокоматовая, подготовка Q3	Tikkurila G503 «Calla»	13,9 м²

Схема развёрток (М 1:100)

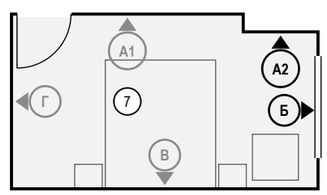

Примечания

1. Размеры — в мм от чистовых поверхностей стен; условные обозначения и общие указания — лист 12.
2. Карнизы (шины) — по ведомости текстиля декоратора: длина L и верх H на развёртке — те же числа, что в ведомости; крепление — до окраски потолка.
3. Линии узора (швы плитки, складки штор, рёбра радиаторов) прерываются у знаков и выносок — просвет между линиями не менее 0,7 мм.
4. Часть марок не уместилась у знаков: коды, высоты и привязки этих позиций — в ведомости точек и выводов под видами.

	Лист	№ док.	Подпись	Дата	Проект: Квартира 68 м², элитный модерн	М 1:20		
Дизайнер	Кырлан А.С.			13.11.26	Развёртки стен А2, Б. Спальня (пом. 7)	Стадия	Лист	Листов
Проверил						П	69	94
Н. контр.								
Утв.								

выпуск 13.11.2026 № c38d47cb31 · стр. 69 из 94

Стена В (М 1:20)


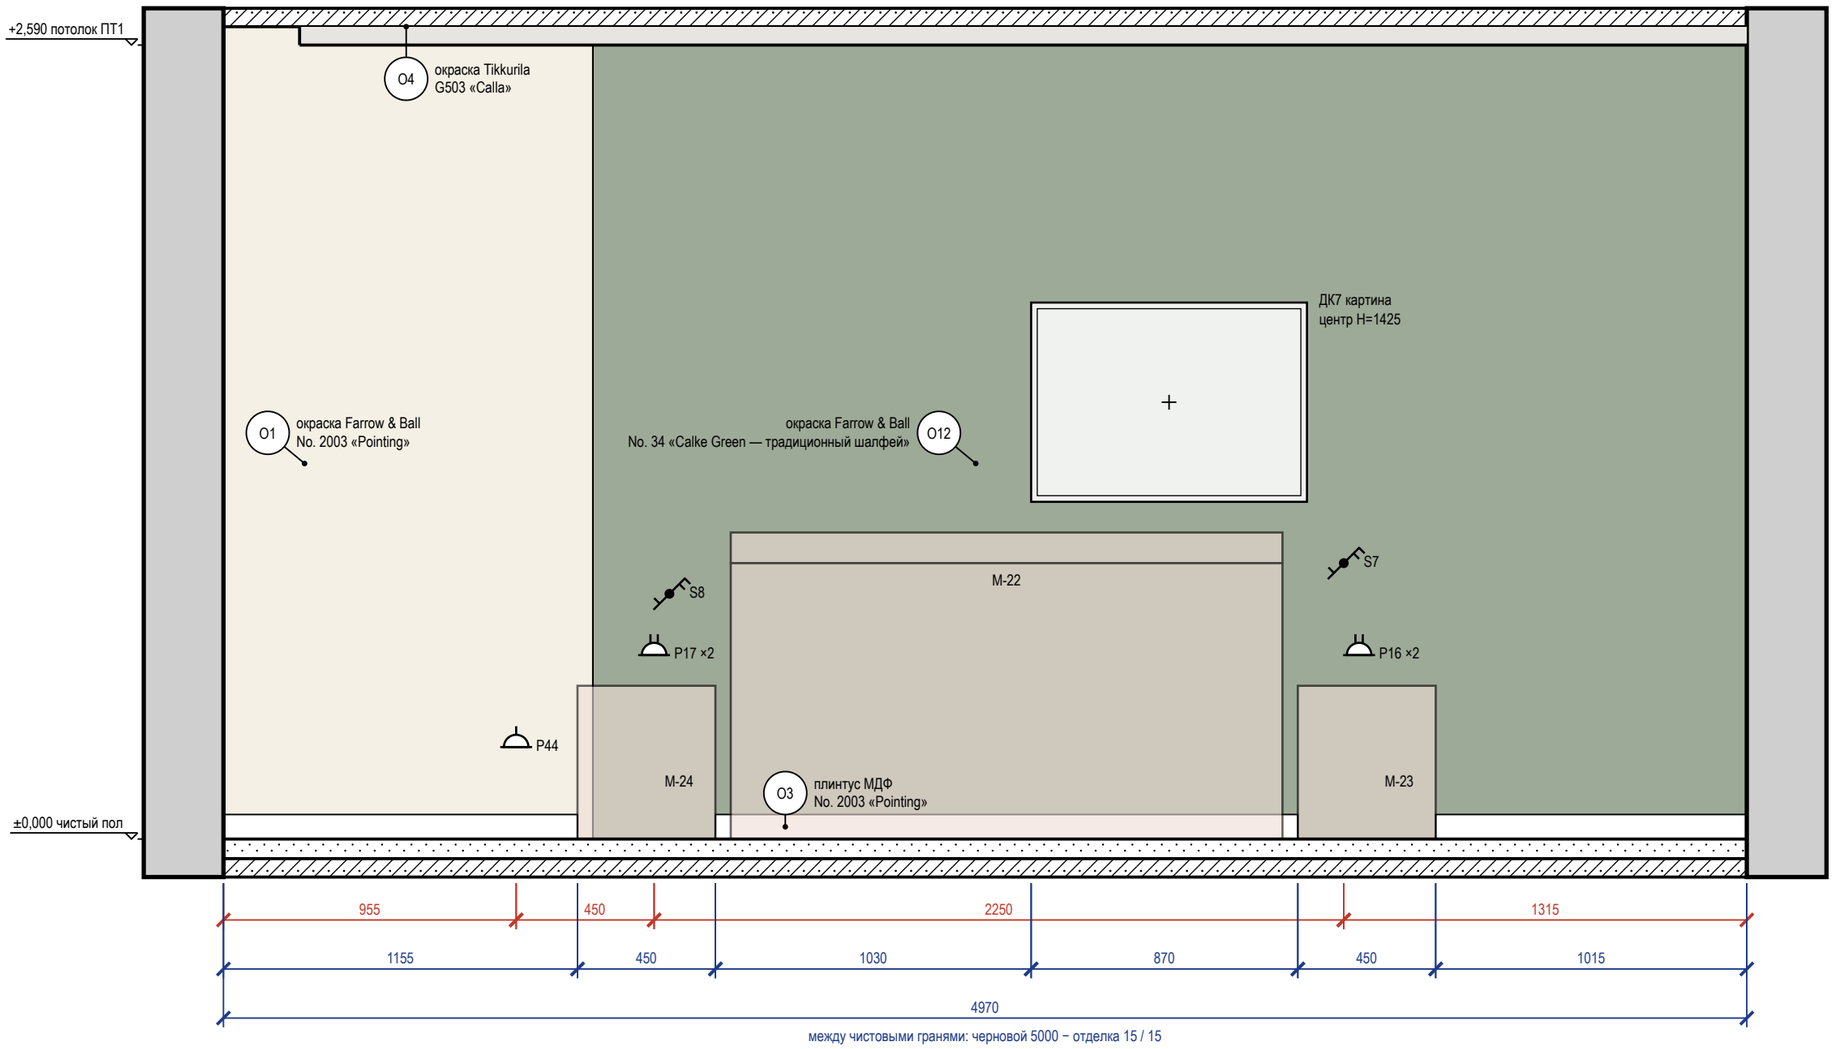



Схема развёрток (М 1:100)

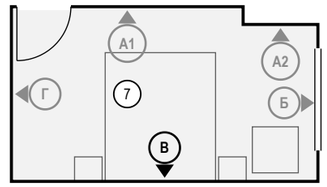

Ведомость точек и выводов

Марка	Что это	Гр.	Н, мм	От угла, мм	Примечание
P44	розетка: общего назначения	6	300	955	
P17	розетка: у кровати: лампа, зарядка	6	600	1405	рамка 2 поста
S8	выключатель	1	800	1455	
S7	выключатель	1	900	3655	
P16	розетка: у кровати: лампа, зарядка	6	600	3705	рамка 2 поста

Стена В — визуализация, лист 11

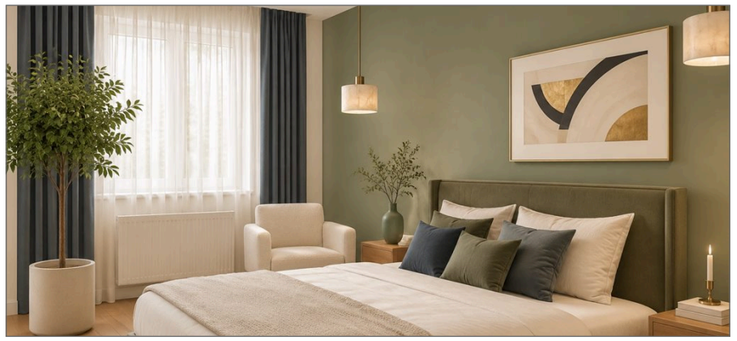

Ведомость изделий и проёмов (на листе)

Марка	Изделие, проём	На виде Ш×В, мм	Низ, мм
М-24	тумба прикроватная правая, дуб натуральный	450×500	0
М-22	кровать 1800×2100, мягкое изголовье до 1300 мм, бархат, латунный кант	1800×900	0
ДК7	картина	900×650	1100
М-23	тумба прикроватная левая, дуб натуральный	450×500	0

Примечания

1. Размеры — в мм от чистовых поверхностей стен; условные обозначения и общие указания — лист 12.
2. Отделка стен — по ведомости отделки помещений, лист С1.
3. Картины и зеркала крепить к основанию по паспорту изделия (закладные и анкеры — в перечне скрытых работ); крест — ось центра предмета.

	Лист	№ док.	Подпись	Дата	Проект: Квартира 68 м², элитный модерн	М 1:20		
Дизайнер	Кырлан А.С.			13.11.26	Развёртка стены В. Спальня (пом. 7)	Стадия	Лист	Листов
Проверил						П	70	94
Н. контр.								
Утв.								

Стена Г (М 1:20)


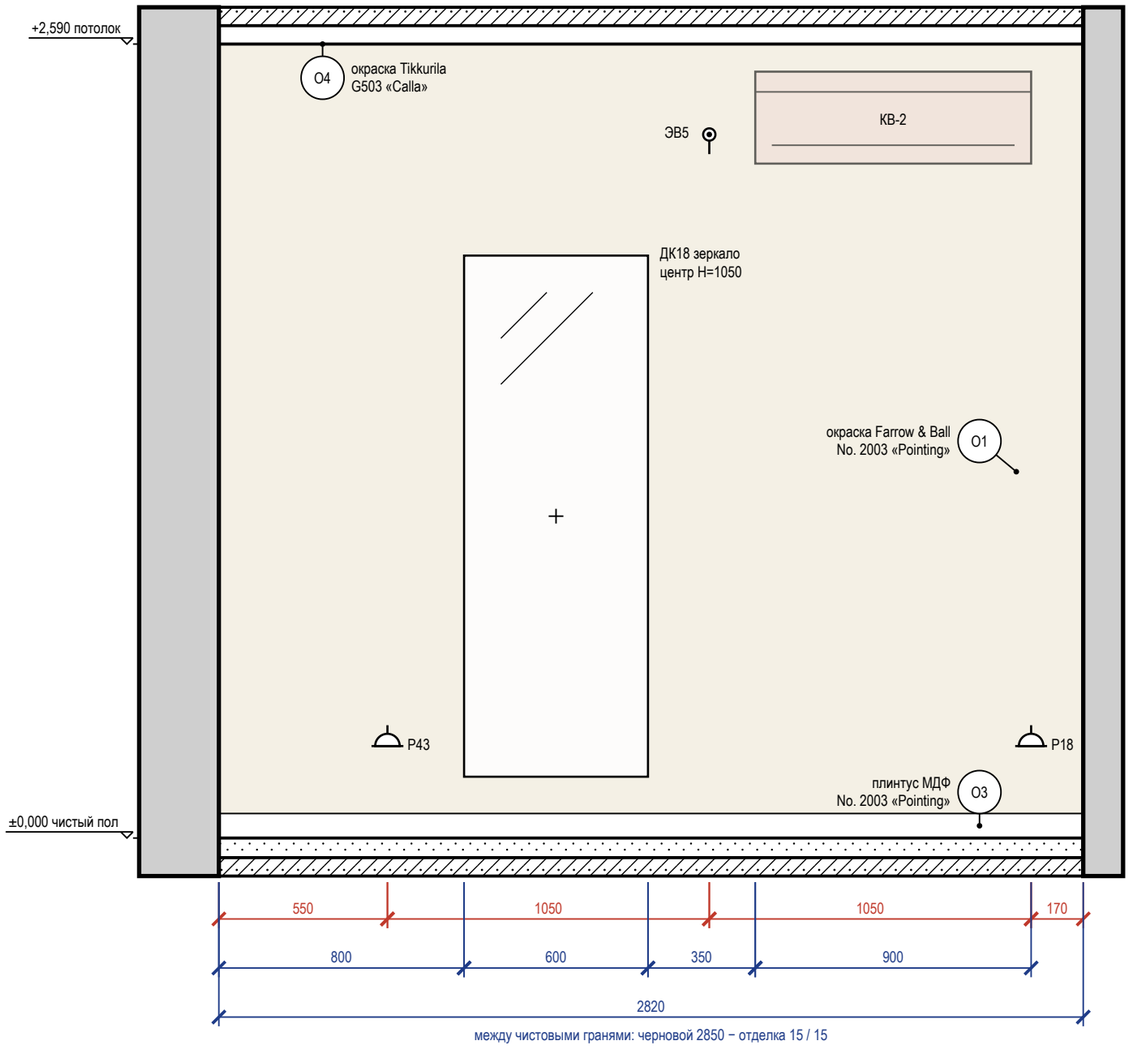


Схема развёрток (М 1:50)

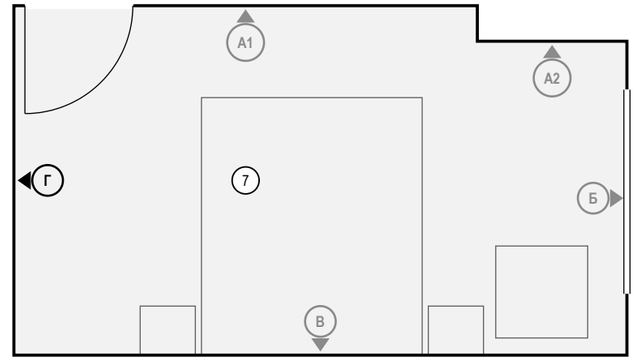

Ведомость точек и выводов

Марка	Что это	Гр.	Н, мм	От угла, мм	Примечание
Р43	розетка: общего назначения	6	300	550	
ЭВ5	вывод кабеля: кондиционер КВ-2 — вывод питания внутреннего блока	18	2295	1600	
Р18	розетка: уборка	6	300	2650	

Ведомость отделки (на листе)

Марка	Поверхность	Материал, изделие	Цвет, код	Кол.
О1	стены	окраска, Farrow & Ball Modern Emulsion, матовая, подготовка Q3	Farrow & Ball No. 2003 «Pointing»	7,3 м²
О3	плинтус	плинтус МДФ, h 80 мм, аналог: плинтус МДФ под покраску 80×16	Farrow & Ball No. 2003 «Pointing»	2,8 м
О4	потолок	окраска, Tikkurila Euro Power 7, глубокоматовая, подготовка Q3	Tikkurila G503 «Calla»	13,9 м²

Ведомость изделий и проёмов (на листе)

Марка	Изделие, проём	На виде Ш×В, мм	Низ, мм
ДК18	зеркало	600×1700	200
КВ-2	кондиционер, внутренний блок	900×300	2200

Примечания

1. Размеры — в мм от чистовых поверхностей стен; условные обозначения и общие указания — лист 12.
2. Картины и зеркала крепить к основанию по паспорту изделия (закладные и анкеры — в перечне скрытых работ); крест — ось центра предмета.

	Лист	№ док.	Подпись	Дата
Дизайнер	Кырлан А.С.			13.11.26
Проверил				
Н. контр.				
Утв.				

Проект: Квартира 68 м², элитный модерн — **М 1:20**

Развёртка стены Г. Спальня (пом. 7)

Стадия	Лист	Листов
П	71	94

выпуск 13.11.2026 № c38d47cb31 · стр. 71 из 94

Комплект предварительный по пунктам этих таблиц. Пока по пункту нет ответа или решения, показанное на указанном листе — допущение проектировщика, а не утверждённое решение.
Сводка: открытых вопросов — 25 (из них ждут факта объекта — 7: контрольного обмера, обследования или документа); изменений в реестре — 8, из них без подписи — 1.

Открытые вопросы и принятые допущения

№	Формулировка	Вид	Кто решает	Если решения нет	Лист, где это проявляется
К-1	Планировка принята по обводу плана заказчика, без обмера: план заказчика распознан автоматически по картинке (1 модель ИИ, масштаб — размерные цепочки), затем исправлен исполнителем вручную по размерным числам и рисунку плана (15 правок) и не проверен дизайнером: положение помещений, стен и проёмов — по обводу, контрольный обмер на объекте не выполнялся. От этого зависят все размеры альбома, площади, заказ материалов и изделий. Нужны план БТИ / проект дома и контрольный обмер; до них планировочное решение заменяется обводом плана и уточняется обмером.	Непонятно Ждёт: документа, обмера	Архитектор-планировщик	размеры и расстановка на листах — предложение проектировщика по брифу; мебель на заказ, двери и материалы по ним не заказывать	л. 14 — План планировки от заказчика л. 37 — План размещения дверей л. 20 — План размещения мебели и оборудования
К-3	Тип дома, конструкция перекрытия и несущие стены в брифе не указаны; проект дома, план БТИ и техническое заключение не переданы. До их получения все существующие стены считаются несущими.	Отсутствует Ждёт: документа	Архитектор-планировщик	все существующие стены считаются несущими; демонтаж и штробление в них не выполняются до технического заключения	л. 14 — План планировки от заказчика полный альбом
К-4	Стояки: на плане потолков есть только знак ∅ в верхнем левом углу ванной (120 мм от стены) — принят за стояк канализации К1 Ø110; стояки В1 и Т3 на плане не показаны и приняты в том же коробе (предложение). Варианты значения знака: стояк / вентканал / вытяжка. Нужен план с инженерией или обмер; от стояков зависят трассы, уклоны и выпуски.	Непонятно Ждёт: обмера	Инженер ВК (вода, канализация)	стояки К1, В1, Т3 в коробе в углу ванной; трассы и уклоны — от них, к монтажу после обмера	л. 26 — План выводов сантехники л. 27 — Схема разводки водопровода и канализации
К-5	Вентканалы в брифе не показаны: приняты у санузла и кухни. От них зависят вытяжка санузла, вытяжка над плитой (до обмера рециркуляция) и короба потолка.	Отсутствует Ждёт: обмера	Инженер ОВ	вытяжка кухни — рециркуляционная; вентилятор санузла по месту канала после обмера	л. 50 — План вентиляции л. 26 — План выводов сантехники
К-6	Разрешённая мощность по ТУ в брифе не указана; принята 10 кВт (квартира с электроплитой). Тип плиты и система заземления в брифе тоже не указаны: приняты электрическая варочная панель и TN-C-S (PE-проводник от ввода) — от них зависят группа плиты, вводной аппарат и защитное заземление. Передать ТУ или справку УК (мощность, система заземления, наличие газа).	Отсутствует Ждёт: документа	Инженер-электрик	щит и группы рассчитаны на 10 кВт, электроплита, TN-C-S; при других ТУ — пересчёт групп варочной панели и духового шкафа, при газе — задание газовику, при TN-C проект заземления	л. 41 — Однолинейная схема щита
К-7	Стиль выбран заказчиком в брифе: Современный (модерн); второй стиль quiet-luxury 40 % — предложение исполнителя (исполнитель, приём заказа 03.11.2026: в рассказе «элитный проект… премиальные материалы» — премиальная составляющая стиля: натуральный камень, широкая доска, шпон, глубокоматовые тёплые нейтрали), не выбор заказчика. Коды палитры подобраны исполнителем по веерам стиля (Современный (контемпорари) + Тихая роскошь (quiet luxury)): стены FarrowBall No. 2003, потолки Tikkurila G503, акценты по комнатам — NCS S 7010-Y50R, NCS S 6020-G70Y, FarrowBall No. 298. Выкрасы не делались. Утвердить стиль и коды по выкрасам.	Спорно Ждёт: решения	Колорист-комплектатор	коды — предложение исполнителя; краску, ткани и фасады не закупать до выкрасов	л. 19 — Колерная карта л. 20 — План размещения мебели и оборудования
К-8	Кухня, шкафы и встроенная техника описаны характеристиками («аналог по характеристикам»): модели не выбраны, ниши под технику — по паспорту выбранной модели. Выбрать технику и утвердить проект кухни.	Спорно Ждёт: решения	Мебельщик	выводы кухонной техники — после утверждения проекта кухни; мебель на заказ не заказывать	полный альбом л. 45 — План розеток и электровыводов
К-9	Состав семьи в брифе не указан (answers.household пуст): принято 2 человека. От числа жильцов зависят обеденная группа, хранение, нагрузка на санузлы и расчётная мощность. Уточнить у заказчика.	Отсутствует Ждёт: решения	Дизайнер интерьера	расстановка и расчёты — на 2 человека	л. 20 — План размещения мебели и оборудования л. 41 — Однолинейная схема щита
К-10	Заказчик указал в брифе, что плана нет и нужен обмер: все размеры альбома до обмера — допущение.	Отсутствует Ждёт: обмера	Архитектор-планировщик	альбом не выдаётся к работам до обмера	л. 14 — План планировки от заказчика
К-14	Эркер кухни обмерен частично: окно 1300 мм, глубина ≈ 570 мм, скос к нижней стене ≈ 45° (на листе не обмерен, по рисунку ≈ 1150 мм, вероятно, тоже остеклён). В альбоме эркер приведён к прямоугольнику ступенькой (площадь сохранена ±0,15 м²), окно на скосе не показано. Нужен обмер эркера: длины граней, углы, окна.	Непонятно Ждёт: решения	Архитектор-планировщик	эркер — ступенькой, окно только на прямой грани; ниша штор по эркеру — по плану потолков (250 мм)	л. 14 — План планировки от заказчика
К-15	В верхней (наружной?) стене кухни на плане два узких разрыва ≈ 130 мм (над лентой 13) с участком стены 650 мм между ними. Это вентканалы, окно или проходы коммуникаций — по плану потолков не понять. В альбоме не показаны.	Непонятно Ждёт: решения	Архитектор-планировщик	не учитываются; кухонный гарнитур вдоль верхней стены до проверки на месте	л. 14 — План планировки от заказчика
К-16	Входная дверь на плане не помечена (марки Д-1…Д-5 — межкомнатные). Принят вход через проём 880 мм в нижней стене прихожей (единственный разрыв наружной стены без окна).	Непонятно Ждёт: решения	Архитектор-планировщик	вход — там; входной блок — по замеру проёма	л. 14 — План планировки от заказчика
К-17	Проём из прихожей в спальню (880 мм) без марки Д — это проём без двери или дверь, не попавшая в ведомость Д? Варианты: (1) дверь 800 с полотном, как остальные; (2) открытый проём. Рекомендация — (1): спальня не проходная.	Непонятно Ждёт: решения	Архитектор-планировщик	дверь 800 × 2100 с полотном, открывание в спальню	л. 14 — План планировки от заказчика
К-18	В правом верхнем углу спальни прямоугольник ≈ 1300 × 290 мм вне контура потолка (без подписи): короб, шахта, пилон или шкаф. В альбоме — вне помещения.	Непонятно Ждёт: решения	Архитектор-планировщик	участок вне помещения, мебель к нему не ставится	л. 14 — План планировки от заказчика

	Лист	№ док.	Подпись	Дата	Проект: Квартира 68 м², элитный модерн			
Дизайнер	Кырлан А.С.			13.11.26	Открытые вопросы, принятые допущения и конфликты. Лист 1 из 3	Стадия	Лист	Листов
Проверил						П	72	94
Н. контр.								
Утв.								

выпуск 13.11.2026 № c38d47cb31 · стр. 72 из 94

Открытые вопросы и принятые допущения (продолжение)

№	Формулировка	Вид	Кто решает	Если решения нет	Лист, где это проявляется
К-19	У левой стены кухни рядом с Д-4 на плане синий участок «залізобетон» ≈ 640 × 90 мм (выступ стены, ригель или колонна?). В альбоме не показан.	Непонятно Ждёт: решения	Архитектор-планировщик	не учитывается до обмера	л. 14 — План планировки от заказчика
К-20	Светильники перенесены с исходного плана: марки 01-А, 01-Б, 02, 03, 04, 05, 06-А, 06-Б, 08-А, 08-Б, 09, 10, 12 (бра), 13 (подсветка рабочей поверхности), 13-А, 13-Б, 14 и вентиляторы 11 — место по плану (±30 мм по рисунку), но ведомости светильников нет: тип, мощность, световой поток, цвет света не заданы. Приняты: точечные LED 7 Вт 3000 K Ra ≥ 90; 13-А/13-Б — подвесные у кровати; 12 — настенное бра h 1200 (высота не задана); 09 в чёрной нише — трековые/точечные. Марка 13 на плане двойная: «13 підсвітка роб. пов.» в кухне и «13-А/13-Б» в спальне. Нужны ведомость светильников и схема включения (группы А/Б?).	Непонятно Ждёт: решения	Инженер-электрик	светильники по марке плана с параметрами-допущениями; закупать только после ведомости	л. 47 — План освещения
К-21	Ниша в прихожей «покрасить в чорний (темно-сірий)» — кода цвета нет. Предложение: RAL 7016 (антрацит, из палитры стиля), глубокоматовая. Варианты: RAL 9005 (чёрный) / RAL 7016 / NCS S 8500-N. Потолки по плану — RAL 9010.	Непонятно Ждёт: решения	Колорист-комплектатор	RAL 7016 глубокоматовая; выкрас до покраски	л. 19 — Колерная карта
К-22	Сверка с ведомостью отделки потолка заказчика: по альбому ГКЛ 61,14 м² (в ведомости 60,14), ГКЛ влагостойкий 5,81 (3,83 санузел + ванная по размерам больше), шпаклёвка по ж/б 1,52 (4,08 — ниши по размерам меньше), всего 68,47 (68,05). Возможно, в ведомости санузел или его часть посчитан «по ж/б», а ниша штор эркера — со скосом. Какая ведомость верна — по обмеру; ведомость заказчика не подгоняется.	Спорно Ждёт: решения	Гипсокартонщик	объёмы — по чертежу альбома; перед закупкой — по обмеру	л. 38 — План потолков
К-23	Бюджет в брифе не указан («элитный проект, премиальные материалы» — уровень, не сумма). Смета посчитана по премиальным позициям стиля без потолка суммы.	Отсутствует Ждёт: решения	Сметчик	материалы премиум-уровня стиля; сумма — для согласования, не обязательство	полный альбом
К-24	Расчётная нагрузка 10,8 кВт (по коэффициентам спроса, без подгонки) больше принятой разрешённой 10 кВт (К-6; ТУ не переданы). Предложение: запросить у сетевой организации / УК увеличение выделенной мощности до 15 кВт — иначе электроплита, тёплый пол и кондиционеры одновременно не работают; либо снять часть нагрузки (тёплый пол, кондиционеры — они предложены по умолчанию).	Спорно Ждёт: решения	Инженер-электрик	щит собран на 10 кВт, расчётная выше разрешённой; тёплый пол и кондиционеры — предложения, к монтажу не принимать до ответа по мощности	л. 41 — Однолинейная схема щита
К-25	Узел ввода воды принят по умолчанию (предложение): на ХВС и ГВС — кран → фильтр грубой очистки → счётчик → обратный клапан → редуктор давления → кран с электроприводом (защита от протечек) → коллектор на 13 выходов; разводка — коллекторная, в стяжке пола, отдельной трубой к каждому прибору, без соединений в полу. Не известны: место узла и коллектора, давление на вводе, Ду вводов, наличие счётчиков и разрешённый способ учёта (УК) — положение стояков принято без обмера (К-4). Нужны обмер, справка УК и решение по составу узла.	Отсутствует Ждёт: решения	Инженер ВК (вода, канализация)	узел ввода, коллектор и электрокраны — предложение, место на листах условное; трубы и арматуру не закупать, штробы и закладные в стяжке не делать до обмера и решения	л. 27 — Схема разводки водопровода и канализации л. 26 — План выводов сантехники
К-26	Климатический подрайон (СП 131.13330) не задан: принят не северный — жилые комнаты и кухня под потолком от 2,5 м (СП 54, п. 5.12); в IA, IБ, IГ, IД, IVA — от 2,7 м.	Отсутствует Ждёт: документа	Архитектор-планировщик	отметки потолков жилых — по 2,5 м; при северном подрайоне уровни ниже 2,7 м пересчитать до заказа каркаса	л. 38 — План потолков
К-27	Унитаз подвесной С-01 (пом. 2 «Санузел»), выпуск К1-1 Ø110: выпуск Ø110 на высоте 220 мм в инсталляции; трасса до Ст К1-1 задана «в полу», а в пол она не помещается (нужно 210 мм при пироге 90 мм). Рекомендация исполнителя — короб 170×140 над чистым полом вдоль стен до Ст К1-1 (1,26 м): плитка обходит короб, у двери короб не проходит; это штатная прокладка для подвесного прибора: отвод идёт за инсталляцией и в коробе, пол не поднимается. Варианты: (а) короб 170×140 над чистым полом вдоль стен до Ст К1-1 (1,26 м): плитка обходит короб, у двери короб не проходит; (б) подиум или подъём пола на 120 мм — ступень и порог у входа, высота двери в свету и выводов прибора меняются, пересчёт раскладки плитки; (в) прибор ближе к стояку Ст К1-1 — меняется планировка санузла (расстановка, выводы, раскладка); (г) насосная установка (КНС) у прибора — шум, обслуживание, электропитание, согласование; только если другие варианты невозможны. Решение меняет санузел (высоты, раскладку плитки) — за автором с заказчиком.	Спорно Ждёт: решения	Инженер ВК (вода, канализация)	выпуск К1-1 и прибор С-01 не выполнять до решения; остальное — по листам	л. 27 — Схема разводки водопровода и канализации л. 26 — План выводов сантехники
К-28	Ванна С-04 (пом. 3 «Ванная»), выпуск К1-3 Ø50: в полу не помещается: врезка + перепад 62 (2,06 м × 30 мм/м) + Ø50 + слой над трубой 45 = 187 мм при пироге 90 мм. Рекомендация исполнителя — короб 150×110 над чистым полом вдоль стен до Ст К1-1 (2,06 м): плитка обходит короб, у двери короб не проходит; сифон и выпуск прибора — над полом за экраном/корпусом. Варианты: (а) короб 150×110 над чистым полом вдоль стен до Ст К1-1 (2,06 м): плитка обходит короб, у двери короб не проходит; (б) подиум или подъём пола на 100 мм — ступень и порог у входа, высота двери в свету и выводов прибора меняются, пересчёт раскладки плитки; (в) прибор ближе к стояку Ст К1-1 — меняется планировка санузла (расстановка, выводы, раскладка); (г) насосная установка (КНС) у прибора — шум, обслуживание, электропитание, согласование; только если другие варианты невозможны. Решение меняет санузел (высоты, раскладку плитки) — за автором с заказчиком.	Спорно Ждёт: решения	Инженер ВК (вода, канализация)	выпуск К1-3 и прибор С-04 не выполнять до решения; остальное — по листам	л. 27 — Схема разводки водопровода и канализации л. 26 — План выводов сантехники
К-29	Циркуляция ГВС в данных не задана — циркуляционного трубопровода на схеме нет. Решить: нужна ли циркуляция	Отсутствует Ждёт: решения	Инженер ВК (вода, канализация)	циркуляции на схеме нет	л. 31–33 — Развёртки мокрых зон: выводы ВК. Санузел л. 28 — Аксонометрическая схема В1 (холодное водоснабжение) л. 27 — Схема разводки водопровода и канализации

	Лист	№ док.	Подпись	Дата	Проект: Квартира 68 м², элитный модерн			
Дизайнер	Кырлан А.С.			13.11.26	Открытые вопросы, принятые допущения и конфликты. Лист 2 из 3	Стадия	Лист	Листов
Проверил						П	73	94
Н. контр.								
Утв.								

Изменения проекта после выпуска листов (реестр изменений)


№	Дата	Лист	Было	Стало	Кто решил, подпись
ИЗ-1	03.11.2026	л. 14 — План планировки от заказчика л. 38 — План потолков	Высота до плиты 2745 мм — по отметке +2.745 плана потолков (К-2).	Решение автора: от чистого пола до плиты 2650 мм; отметки плана −95 мм, перепады сохранены: по плите +2.650, комнаты +2.590, прихожая +2.550, санузел и ванная +2.505. Датум отметок плана — допущение (отдельный вопрос).	Утверждено: Кырлан А.С., 03.11.2026. Предложил: Александр Кырлан, решение автора.
ИЗ-2	03.11.2026	л. 20 — План размещения мебели и оборудования	Назначение помещений не подписано (К-11).	Решение автора — по предложению исполнителя: кабинет у окна (бра 12), кухня-столовая с эркером (подсветка 13), гостиная, спальня (подвесы 13-А/13-Б, кровать 1800 между ними).	Утверждено: Кырлан А.С., 03.11.2026. Предложил: Александр Кырлан, решение автора.
ИЗ-3	03.11.2026	л. 26 — План выводов сантехники л. 53 — Раскладка плитки. Планы полов	Ванная и санузел не подписаны (К-12).	Решение автора: большее — ванная (ванна 1700 у правой стены, умывальник на тумбе 800, стиральная машина 600 × 600 с выводами и розеткой на своей группе); меньшее — санузел (подвесной унитаз, гигиенический душ, раковина 400).	Утверждено: Кырлан А.С., 03.11.2026. Предложил: Александр Кырлан, решение автора.
ИЗ-4	03.11.2026	полный альбом	Несущие стены не известны (К-13).	Решение автора: все существующие стены — несущие до техзаключения; демонтаж и штробление — после него.	Утверждено: Кырлан А.С., 03.11.2026. Предложил: Александр Кырлан, решение автора.
ИЗ-5	03.11.2026	л. 47 — План освещения л. 38 — План потолков	Споты 70 мм в 60 мм запотолочного (К-31).	Решение: встраиваемые светильники тонкие, монтажная глубина ≤ 50 мм; марки исходного плана сохранены; тип — в спецификации с пометкой «глубина ≤ 50 мм».	Утверждено: Кырлан А.С., 03.11.2026. Предложил: Александр Кырлан, решение автора.
ИЗ-6	03.11.2026	л. 50 — План вентиляции	Вентилятор 11 в потолке мокрых: 145 < 150 мм (К-32).	Решение: вытяжная решётка на стене санузла и ванной в канал, вентилятор канальный настенный с обратным клапаном; знак 11 плана — не в потолке.	Утверждено: Кырлан А.С., 03.11.2026. Предложил: Александр Кырлан, решение автора.
ИЗ-7	03.11.2026	л. 14 — План планировки от заказчика	Датум отметок плана не известен (К-30).	Решение: допущение сохраняется — отметки дизайнера на 95 мм ниже чистого пола; подтвердить на обмере (не блокирует выпуск).	Утверждено: Кырлан А.С., 03.11.2026. Предложил: Александр Кырлан, решение автора.
ИЗ-8	12.11.2026	полный альбом л. 47 — План освещения л. 20 — План размещения мебели и оборудования	Разбор двух критиков по кадрам: «элитный модерн не читается» — дорого выглядят только кухня и умывальник, гостиная и кабинет — типовая квартира, авторского света нет, санузлы пустые. В данных: в гостиной нет журнального стола и кресла, в кабинете — рабочего кресла; светильники — только споты плана потолков, одно бра и два подвеса без наименований; подвес L5 над столом назван у выключателя S3, а точки нет; панели ТВ-стены есть только в наименовании ОБ-03. Противоречия позиций: стол М-01 «шпон ореха, латунные опоры» при полях «дуб» и чёрный металл; ТВ-стена ОБ-03 и консоль М-19 — «шпон ореха» при поле «дуб»; картины ДК4, ДК5, ДК7 — «в латунной раме, рама — дуб», у всех трёх один сюжет, у ДК5 в наименовании «фотография города в дожде»; умывальник С-05 — тумба одновременно «на ножках» и «подвесная»; текстиль — в наименованиях бархат, бордо, шалфей, терракота, в полях лён и нейтральные цвета; подушек 5 на диван и 5 на кровать; монстера ДК8 стояла на тумбе М-24 и углу кровати.	Противоречия сняты: М-01, ОБ-03, М-19 — орех и латунь; стеллаж М-02 — встроенный, шпон ореха и латунь; С-05 — тумба подвесная; зеркало ДК1 — латунная рама; картины ДК4 (абстракция), ДК5 (горный пейзаж), ДК7 (графика дугами) — латунные рамы, у каждой свой сюжет, без людей и городов. Текстиль приведён к наименованиям: портьеры — бархат (кабинет — светлый серо-бежевый, гостиная — шалфей, спальня — чернильный синий), подушки 2 + 2 (гостиная: бархат бордо и жаккард шалфей; спальня: бархат шалфей и жаккард синий), пледы и ковры — в тонах палитры; бордо No. 43 в текстиле — осознанный акцент палитры проекта. Свет: люстры-подвесы в кабинете (L17, клавиша 2 у S1) и гостиной (L15, клавиша 2 у S6), подсветка картины ДК4 (L16, клавиша 2 у S5), подвес над обеденным столом (L5, клавиша 2 у S3); бра Св7 и подвесы Св58, Св59 получили наименования (латунь, матовое стекло, алебастр). Гостиная: журнальный стол М-20 (мрамор, латунь), кресло М-21 (бархат бордо; 345 мм до радиатора РО-3), панели шпона ореха на ТВ-стене (ДС1), книги и керамика на столе, лампа и керамика на консоли; между диваном и столом 500 мм, между столом и ТВ-тумбой 625 мм. Кабинет: рабочее кресло М-03 (сдвинуто к правому краю стола — перед столом свободно 900 мм), ковёр, картина над столом и абстракция на стене В, настольная лампа; кресло для чтения не задано — перекрывает проход у полотна двери Д-1. Спальня: кресло М-25 в эркере, зеркало в рост, книги и керамика на тумбах, монстера ДК8 перенесена в эркер. Кухня: керамика на столешнице. Санузел: ваза и свеча на полке короба инсталляции, графика на стене Б. Ванная: полотенца для рук и керамика на тумбе, свеча на бортике ванны; коврик не задан — свободный пол перед ванной заметает полотно двери Д-3 и дверца стиральной машины; полотенцесушителя в данных ванной нет — банные полотенца не заданы. Прихожая: свободных стен нет (двери, щиты, домофон) — добавлений нет. Знак «**» у позиций до подписи автора.	Не утверждено: подписи нет. решение исполнителя; предложение проектировщика, на утверждение А. С. Кырлана

Примечания


1. Номера листов — по ведомости рабочих чертежей комплекта (лист «Общие данные»).
2. Графа «Если решения нет» показывает состояние решения на листах; влияние на сроки и стоимость по пунктам не оценивалось.
3. Пункт, по которому принято решение, при следующем выпуске комплекта из таблиц исключается.

	Лист	№ док.	Подпись	Дата	Проект: Квартира 68 м², элитный модерн			
Дизайнер	Кырлан А.С.			13.11.26	Открытые вопросы, принятые допущения и конфликты. Лист 3 из 3	Стадия	Лист	Листов
Проверил						П	74	94
Н. контр.								
Утв.								


Вид с фасадами (М 1:20)

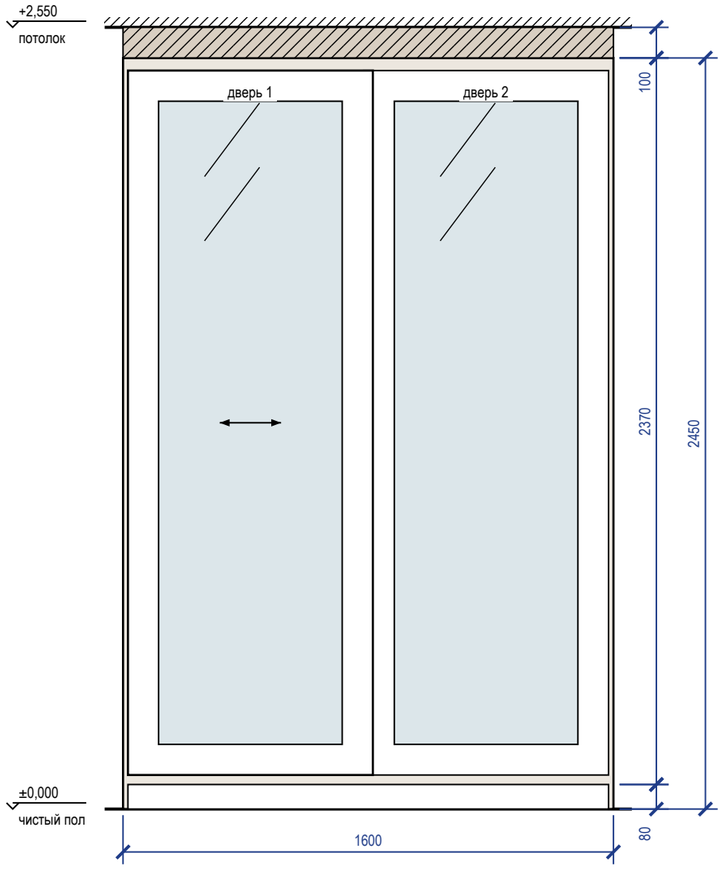


Вид без фасадов (М 1:20)

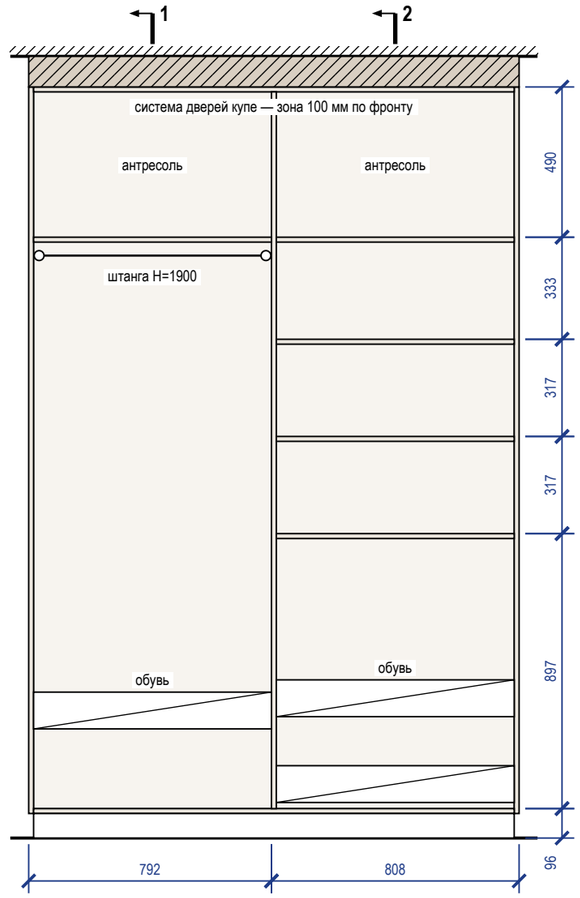

Разрез 1-1 (М 1:20)

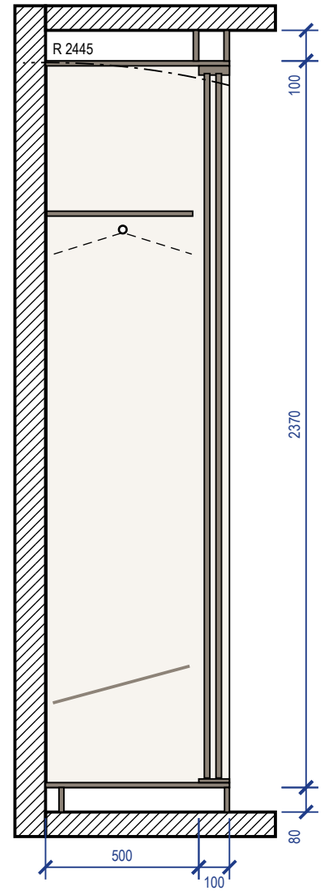


Разрез 2-2 (М 1:20)

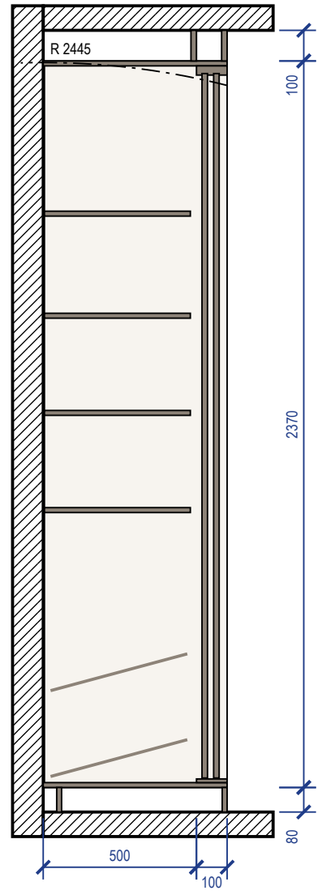

Примечания

1. Размеры — в мм по чистовой отделке; изделие 1600×600×2450 (Ш×Г×В). Перед раскроем — контрольный замер цеха после чистовой отделки стен, пола и потолка.
2. Корпус — ЛДСП 16 мм, задняя стенка ХДФ 4 мм в паз, цоколь 80 мм на регулируемых опорах; двери купе — МДФ, шпон / эмаль 18 мм; вставка — зеркало серебро 4 мм на безопасной плёнке, в профиле двери; нахлёст 30 мм, ширина двери 799 мм, высота — проём минус 40 мм; цвет — по колерной карте.
3. Кромка: скрытые торцы 0,4 мм, видимые 1 мм (ПВХ/АБС).
4. Номинальные зазоры: дверь купе — боковина 3 мм, фасад ящика — стойка 2 мм; ящики внутри купе — с накладкой 30 мм на стойке со стороны нахлёста дверей.
5. Присадка по 32-й системе — выполняет цех.
6. Компенсатор 100 мм — короб из ЛДСП по фронту и торцам, подгоняется к потолку при монтаже (припуск 20 мм), крепится к корпусу и к потолку.
7. Подъём корпуса: диагональ боковины без цоколя $\sqrt{(2370^2 + 600^2)} = 2445$ мм < 2550 мм до потолка — корпус собирается лёжа, поднимается поворотом и ставится на цоколь.
8. Крепление к стене от опрокидывания — уголки 2 шт. к несущему основанию (монтажная схема шкафов).


3D орто

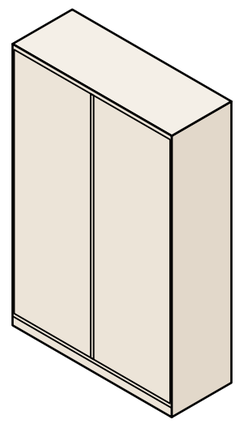


	Лист	№ док.	Подпись	Дата	Проект: Квартира 68 м², элитный модерн			М 1:20
Дизайнер	Кырлан А.С.			13.11.26	Шкаф-купе М-04	Стадия	Лист	Листов
Проверил						П	Д1	94
Н. контр.								
Утв.								

выпуск 13.11.2026 № c38d47cb31 · стр. 75 из 94


Вид с фасадами (М 1:25)

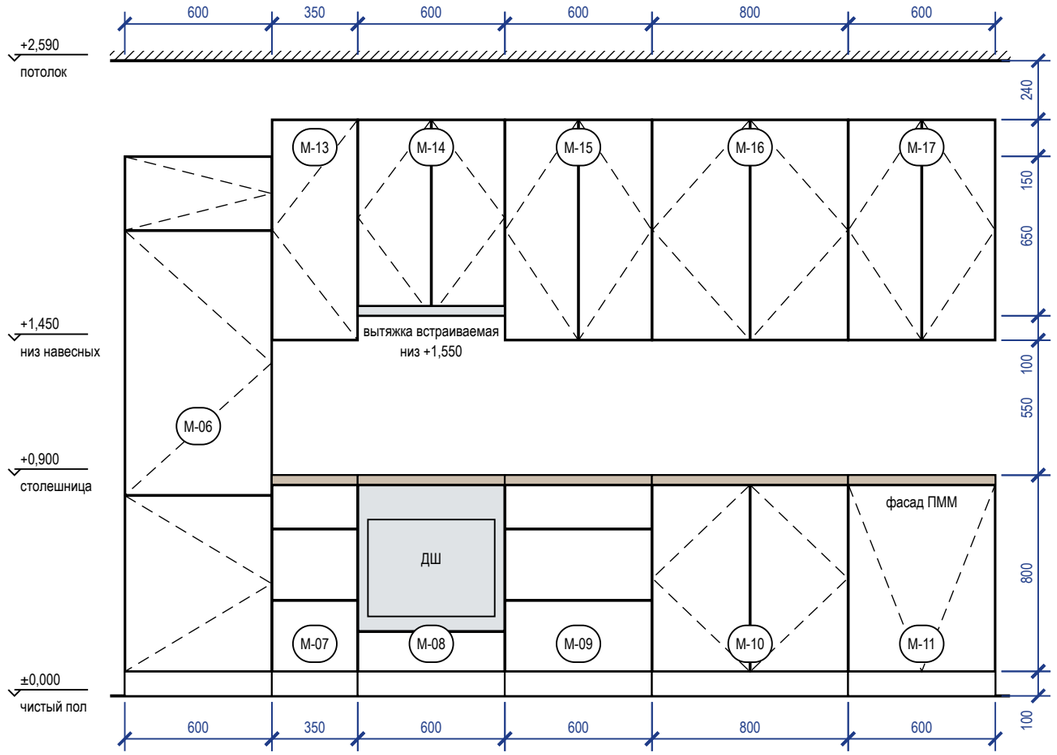


Вид без фасадов: наполнение, выводы (М 1:25)

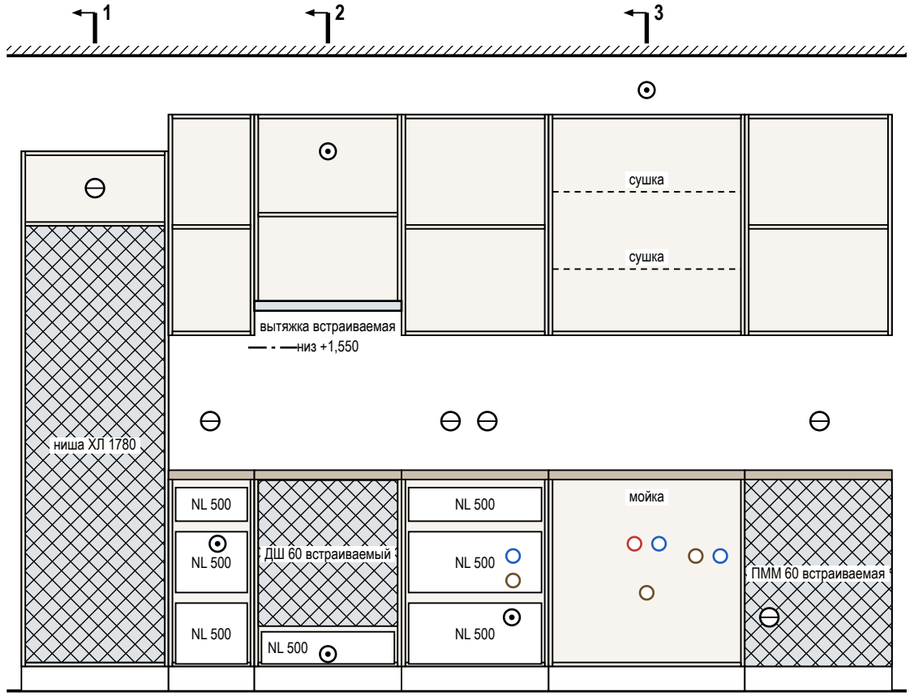


Разрез 1-1 (М 1:25)

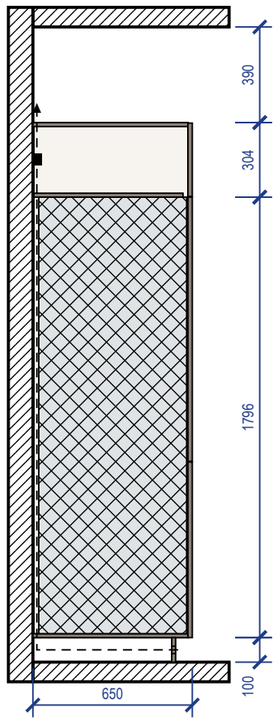


Разрез 2-2 (М 1:25)

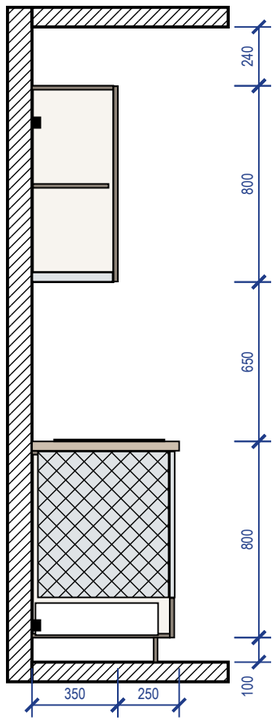

Разрез 3-3 (М 1:25)

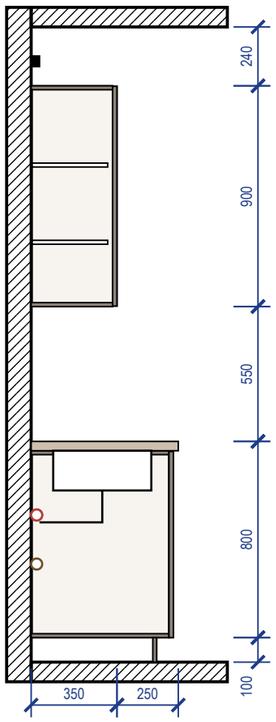

3D орто

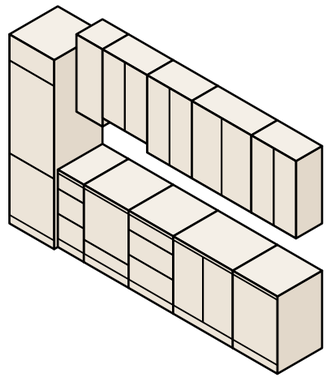

Примечания

1. Размеры — в мм по чистовой отделке, вид из помещения; марки — как на плане расстановки. Перед раскроем — контрольный замер цеха после фартука и пола.
2. Корпуса — ЛДСП 16 мм, задняя стенка ХДФ 4 мм; фасады — МДФ, шпон американского ореха, фрезеровка-рейка 30 мм, скрытые петли 18 мм, цвет по колерной карте; столешница 38 мм, свес 20 мм; цоколь 100 мм.
3. Кромка: скрытые торцы 0,4 мм, видимые 1 мм. Номинальные зазоры: между фасадами 3 мм, фасад — столешница 3 мм, фасад — стена не менее 3 мм.
4. Ящики полного выдвижения и петли — с доводчиком; присадка по 32-й системе — выполняет цех.
5. Наименования и габариты модулей (М…) — в ведомости изделий, лист 25.
6. Вытяжка встраивается в дно навесного модуля М-14 над варочной: её низ на 1550 мм от пола, 650 мм над панелью (не меньше 650 мм).
7. Ниши техники (холодильник — ориентир 1780 мм) — по монтажным схемам выбранных моделей: решётка в цоколе и канал за пеналом холодильника, зазор за духовым шкафом, фасад ПММ на двери машины.

	Лист	№ док.	Подпись	Дата	Проект: Квартира 68 м², элитный модерн			М 1:25
Дизайнер	Кырлан А.С.			13.11.26	Кухня (пом. 5). Развёртка гарнитура	Стадия	Лист	Листов
Проверил						П	Д2	94
Н. контр.								
Утв.								

выпуск 13.11.2026 № c38d47cb31 · стр. 76 из 94

Ведомость отделки помещений (форма 1 прил. А ГОСТ 21.501-2018). Лист 1 из 2

№	Наименование помещения	Потолок			Стены и перегородки			Низ стен (плинтус)			Пол		Примечание
		Вид отделки	Код цвета	S, м²	Вид отделки	Код цвета	S, м²	Вид отделки	Код цвета	L, м	Вид отделки	S, м²	
1	Кабинет 10,61 м²	ГКЛ по каркасу П113, отм. +2,590; окраска, Tikkurila Euro Power 7, глубокоматовая, 2 слоя, подготовка Q3	Tikkurila G503	10,61	Окраска, Farrow & Ball Modern Emulsion, матовая, 2 слоя, подготовка Q3 Акцент — стена B: окраска, Tikkurila Euro Power 7, колеровка по NCS, матовая, 2 слоя, подготовка Q3	Farrow & Ball No. 2003 Farrow & Ball No. 30	20,12 9,60	Плинтус МДФ h=80 мм, аналог: МДФ под покраску 80×16	Farrow & Ball No. 2003	12,3	Аналог: инженерная доска, дуб натуральный, масло, 1-полосная, 14/4 мм, на клею; тип 1, отм. ЧП ±0,000	10,61	Н стен 2590 (до потолка); плинтус в цвет: стены
2	Санузел 1,85 м²	ГКЛВ по каркасу П113, отм. +2,505; окраска, Tikkurila Euro Power 7, матовая, 2 слоя, подготовка Q3	Tikkurila G503	1,85	Облицовка плиткой, аналог: керамогранит под травертин, матовый, 600×1200×9 мм, клей C2 TE S1, затирка CG2WA	по артикулу	11,76	нет			Аналог: керамогранит ректифицированный под травертин, матовый, 600×600×9 мм; тип 2, отм. ЧП −0,015	1,85	Н стен 2520 (до потолка); тёплый пол; гидроизоляция обмазочная, 2 слоя, с заведением на стены 200 мм (по пирогу пола); тест проливом и акт скрытых работ
3	Ванная 3,96 м²	ГКЛВ по каркасу П113, отм. +2,505; окраска, Tikkurila Euro Power 7, матовая, 2 слоя, подготовка Q3	Tikkurila G503	3,96	Облицовка плиткой, аналог: керамогранит под травертин, матовый, 600×1200×9 мм, клей C2 TE S1, затирка CG2WA	по артикулу	17,72	нет			Аналог: керамогранит ректифицированный под травертин, матовый, 600×600×9 мм; тип 2, отм. ЧП −0,015	3,96	Н стен 2520 (до потолка); тёплый пол; гидроизоляция обмазочная, 2 слоя, с заведением на стены 200 мм; над ванной — до 2000 и 300 мм за борт (по пирогу пола); тест проливом и акт скрытых работ
4	Прихожая 13,87 м²	ГКЛ/Существующий потолок по каркасу П113, отм. +2,550; +2,650; окраска, Tikkurila Euro Power 7, глубокоматовая, 2 слоя, подготовка Q3	Tikkurila G503	13,87	Окраска, Farrow & Ball Modern Emulsion, матовая, 2 слоя, подготовка Q3	Farrow & Ball No. 2003	23,50	Плинтус МДФ h=80 мм, аналог: МДФ под покраску 80×16	Farrow & Ball No. 2003	9,8	Аналог: керамогранит ректифицированный под травертин, матовый, 600×1200×9 мм; тип 3, отм. ЧП ±0,000	13,87	Н стен 2550 (до потолка); за встроенной мебелью до потолка (4,08 м²) финишной отделки нет — подготовка и грунт под мебель; тёплый пол; матовая моющаяся, класс 1 EN 13300 осознанно вместо полуматовой; плинтус в цвет: стены

Примечания

1. Ведомость продолжена на листе 2 из 2; итоги, сводка площадей и примечания — на последнем листе ведомости.

	Лист	№ док.	Подпись	Дата	Проект: Квартира 68 м², элитный модерн			
Дизайнер	Кырлан А.С.			13.11.26	Ведомость отделки помещений. Лист 1 из 2	Стадия	Лист	Листов
Проверил						П	С1	94
Н. контр.								
Утв.								

Ведомость отделки помещений (форма 1 прил. А ГОСТ 21.501-2018). Лист 2 из 2

№	Наименование помещения	Потолок			Стены и перегородки			Низ стен (плинтус)			Пол		Примечание
		Вид отделки	Код цвета	S, м²	Вид отделки	Код цвета	S, м²	Вид отделки	Код цвета	L, м	Вид отделки	S, м²	
5	Кухня-столовая 12,04 м²	ГКЛ по каркасу П113, отм. +2,590; окраска, Tikkurila Euro Power 7, глубокоматовая, 2 слоя, подготовка Q3	Tikkurila G503	12,04	Окраска, Farrow & Ball Modern Emulsion, матовая, 2 слоя, подготовка Q3 Акцент — стена В: окраска, Tikkurila Euro Power 7, колеровка по NCS, матовая, 2 слоя, подготовка Q3 Фартук кухни (стена А): облицовка керамогранитом, аналог: керамогранит под травертин, матовый, 1200×600×9 мм, клей C2 TE S1, затирка CG2WA	Farrow & Ball No. 2003 Farrow & Ball No. 281 по артикулу	22,56 9,96 1,68	Плинтус МДФ h=80 мм, аналог: МДФ под покраску 80×16	Farrow & Ball No. 2003	13,8	Аналог: инженерная доска, дуб натуральный, масло, 1-полосная, 14/4 мм, на клею; тип 1, отм. ЧП ±0,000	12,04	Н стен 2590 (до потолка); матовая моющаяся, класс 1 EN 13300 — осознанно вместо полуматовой; плинтус в цвет: стены
6	Гостиная 12,24 м²	ГКЛ по каркасу П113, отм. +2,590; окраска, Tikkurila Euro Power 7, глубокоматовая, 2 слоя, подготовка Q3	Tikkurila G503	12,24	Окраска, Farrow & Ball Modern Emulsion, матовая, 2 слоя, подготовка Q3 Акцент — стена А: окраска, Farrow & Ball Modern Emulsion, матовая, 2 слоя, подготовка Q3	Farrow & Ball No. 2003 Farrow & Ball No. 43	22,36 9,92	Плинтус МДФ h=80 мм, аналог: МДФ под покраску 80×16	Farrow & Ball No. 2003	13,3	Аналог: инженерная доска, дуб натуральный, масло, 1-полосная, 14/4 мм, на клею; тип 1, отм. ЧП ±0,000	12,24	Н стен 2590 (до потолка); плинтус в цвет: стены
7	Спальня 13,90 м²	ГКЛ по каркасу П113, отм. +2,590; окраска, Tikkurila Euro Power 7, глубокоматовая, 2 слоя, подготовка Q3	Tikkurila G503	13,90	Окраска, Farrow & Ball Modern Emulsion, матовая, 2 слоя, подготовка Q3 Акцент — стена В: окраска, Farrow & Ball Modern Emulsion, матовая, 2 слоя, подготовка Q3	Farrow & Ball No. 2003 Farrow & Ball No. 34	23,37 12,95	Плинтус МДФ h=80 мм, аналог: МДФ под покраску 80×16	Farrow & Ball No. 2003	14,8	Аналог: инженерная доска, дуб натуральный, масло, 1-полосная, 14/4 мм, на клею; тип 1, отм. ЧП ±0,000	13,90	Н стен 2590 (до потолка); плинтус в цвет: стены
	Итого			**68,47**			**185,48**			**63,9**		**68,47**	

Сводка площадей по материалам отделки

Поверхность	Материал / код цвета	Серия	Площадь, м²
Потолок	Tikkurila G503	Euro Power 7	68,47
Стены	Farrow & Ball No. 2003	Modern Emulsion	111,90
Стены	Farrow & Ball No. 30	Euro Power 7, колеровка по NCS	9,60
Стены	облицовка плиткой 600×1200×9 мм	аналог: керамогранит под травертин, матовый	29,47
Стены	Farrow & Ball No. 281	Euro Power 7, колеровка по NCS	9,96
Стены	Farrow & Ball No. 43	Modern Emulsion	9,92
Стены	Farrow & Ball No. 34	Modern Emulsion	12,95
Фартук	облицовка керамогранитом 1200×600×9 мм	аналог: керамогранит под травертин, матовый	1,68

Примечания

1. Площади поверхностей — по чистым граням стен до отделки: стены = периметр × высоту от чистого пола помещения до низа потолка минус проёмы (облицовка плиткой — до верха облицовки); плинтус = периметр минус дверные проёмы; пол и потолок — по площади помещения. Количество плиток по раскладке. Площади помещений — с учётом всех частей помещения; откосы в площадь стен не входят.
2. Акцентные стены и фартук — отдельными строками, их площадь вычтена из основной отделки стен помещения; фартук — над нижними модулями кухни от столешницы до низа навесных шкафов, где шкафов нет — на 600 мм.
3. Плинтус — длина по периметру за вычетом дверных проёмов; примыкания к наличникам и встроенной мебели — по развёрткам.
4. Формат плитки — Ш×В×Т (ширина × высота в положении укладки × толщина), мм; на полу — вдоль стен А/В × вдоль стен Б/Г.
5. Коды цвета — по веерам производителей; колеровка каждой краски одной партией, проверка выкраса при свете D65 и при лампах проекта.
6. Уровни подготовки Q1–Q4 — система Knauf, не норма ГОСТ/СП; допуски поверхностей — по СП 71.13330.2017 (действующая редакция).
7. «аналог:» — изделие задано характеристиками, марку и артикул согласовать с заказчиком до закупки.

	Лист	№ док.	Подпись	Дата	Проект: Квартира 68 м², элитный модерн			
Дизайнер	Кырлан А.С.			13.11.26	Ведомость отделки помещений. Лист 2 из 2	Стадия	Лист	Листов
Проверил						П	С2	94
Н. контр.								
Утв.								

Поз.	Наименование и техническая характеристика	Тип, марка, обозначение документа	Код продукции	Поставщик	Ед. изм.	Кол.	Образец	Примечание
	Лакокрасочные материалы							
1	Краска интерьерная водно-дисперсионная акриловая для стен, матовая, класс мокрого истирания 1 по EN 13300, база A; цвет по вееру Farrow & Ball No. 2003 «Pointing», колеровка машинная	Farrow & Ball Modern Emulsion		Farrow & Ball	л	32,5		поз. К1 колерной карты; пом. 1, 4, 5, 6, 7; S = 111,9 м² × 2 сл. × 0,12 л/м² = 26,9 л, +10 % и 0,5 л на подкраску → ≥ 30,0 л; тара 6 × 5 л + 1 × 2,5 л
2	Краска интерьерная водно-дисперсионная акриловая для акцентных стен, матовая, класс мокрого истирания 1 по EN 13300, база C; цвет по вееру Farrow & Ball No. 30 «Hague Blue — глубокий сине-зелёный», колеровка машинная	Tikkurila Euro Power 7, колеровка по NCS		Tikkurila	л	5		поз. К2 колерной карты; пом. 1; S = 9,6 м² × 2 сл. × 0,12 л/м² = 2,3 л, +10 % и 0,5 л на подкраску → ≥ 3,0 л; тара 1 × 5 л
3	Краска интерьерная водно-дисперсионная акриловая для потолков, глубокоматовая, класс мокрого истирания 2 по EN 13300, база A; цвет по вееру Tikkurila G503 «Calla», колеровка машинная	Tikkurila Euro Power 7		Tikkurila	л	17,1		поз. К3 колерной карты; пом. 1, 4, 5, 6, 7; S = 62,7 м² × 2 сл. × 0,12 л/м² = 15,0 л, +10 % и 0,5 л на подкраску → ≥ 17,0 л; тара 1 × 9 л + 3 × 2,7 л
4	Краска интерьерная водно-дисперсионная акриловая для потолков, матовая, класс мокрого истирания 1 по EN 13300, база A; цвет по вееру Tikkurila G503 «Calla», колеровка машинная	Tikkurila Euro Power 7		Tikkurila	л	2,7		поз. К5 колерной карты; пом. 2, 3; S = 5,8 м² × 2 сл. × 0,12 л/м² = 1,4 л, +10 % и 0,5 л на подкраску → ≥ 2,0 л; тара 1 × 2,7 л
5	Краска интерьерная водно-дисперсионная акриловая для акцентных стен, матовая, класс мокрого истирания 1 по EN 13300, база C; цвет по вееру Farrow & Ball No. 281 «Stiffkey Blue — чернильный синий», колеровка машинная	Tikkurila Euro Power 7, колеровка по NCS		Tikkurila	л	5		поз. К6 колерной карты; пом. 5; S = 10,0 м² × 2 сл. × 0,12 л/м² = 2,4 л, +10 % и 0,5 л на подкраску → ≥ 3,1 л; тара 1 × 5 л
6	Краска интерьерная водно-дисперсионная акриловая для акцентных стен, матовая, класс мокрого истирания 1 по EN 13300, база C; цвет по вееру Farrow & Ball No. 43 «Eating Room Red — брусничный красный», колеровка машинная	Farrow & Ball Modern Emulsion		Farrow & Ball	л	5		поз. К7 колерной карты; пом. 6; S = 9,9 м² × 2 сл. × 0,12 л/м² = 2,4 л, +10 % и 0,5 л на подкраску → ≥ 3,1 л; тара 1 × 5 л
7	Краска интерьерная водно-дисперсионная акриловая для акцентных стен, матовая, класс мокрого истирания 1 по EN 13300, база C; цвет по вееру Farrow & Ball No. 34 «Calke Green — традиционный шалфей», колеровка машинная	Farrow & Ball Modern Emulsion		Farrow & Ball	л	5		поз. К8 колерной карты; пом. 7; S = 12,9 м² × 2 сл. × 0,12 л/м² = 3,1 л, +10 % и 0,5 л на подкраску → ≥ 3,9 л; тара 1 × 5 л
8	Краска для МДФ и дерева в цвет Farrow & Ball No. 2003 «Pointing» — окраска плинтуса; блеск не ниже блеска стен	марка не задана			л	1,7		поз. К4; пом. 1, 4, 5, 6, 7; L = 63,9 м, S = 6,1 м² × 2 сл. × 0,12 л/м² + 10 %; продукт подобрать в веере Farrow & Ball
9	Грунтовка акриловая под окраску стен и потолков — из системы производителя краски	по системе краски			м²	223		площадь окраски стен, акцентов и потолков; 1 слой перед окраской; расход — по ТУ грунтовки
	Плитка и керамогранит							
10	Керамогранит под травертин, 600×600×9 мм, ректификат, водопоглощение 0,1 % (BIa), противоскольжение R10, PEI IV	аналог по характеристикам			м²	7,56		шов 2 мм; Санузел, пол; Ванная, пол; по раскладке 18 шт (S = 5,81 м²), с запасом 21 шт
11	Керамогранит под травертин, 600×1200×9 мм, ректификат, водопоглощение 0,1 %	аналог по характеристикам			м²	43,92		шов 2 мм; Санузел, стены А–Г; Санузел, короб инсталляции; Ванная, стены А–Г; по раскладке 52 шт (S = 30,23 м²), с запасом 61 шт
12	Керамогранит ректифицированный под травертин, матовый, 600×1200×9 мм, водопоглощение 0,1 % (BIa), противоскольжение R10, PEI IV	аналог по характеристикам			м²	19,44		шов 2 мм; Прихожая, пол; по раскладке 24 шт (S = 13,87 м²), с запасом 27 шт
13	Керамогранит под травертин, матовый, 1200×600×9 мм, ректификат, водопоглощение 0,1 % (BIa)	аналог по характеристикам			м²	4,32		шов 2 мм; Кухня-столовая, фартук (ст. А); по раскладке 5 шт (S = 1,68 м²), с запасом 6 шт
	Напольные покрытия							
14	Инженерная доска, дуб натуральный, масло, 1-полосная, 14/4 мм, эмиссия E1, укладка на клей	аналог по характеристикам			м²	52,5		пом. 1, 5, 6, 7; S = 49,02 м² (пол + половина стены в дверных проёмах, как в смете) + 7 %; к заказу — кратно упаковке
15	Клей для паркета и инженерной доски, эластичный (СМП / полиуретановый)	по рекомендации производителя доски			м²	50		площадь приклейки; расход и шпатель — по ТУ клея
	Погонажные изделия							
16	Плинтус МДФ под покраску 80×16, крепление к стене, окраска в цвет Farrow & Ball No. 2003	аналог по характеристикам			м	71		пом. 1, 4, 5, 6, 7; L = 63,9 м (периметр без дверных проёмов) + 10 % на подрезку; в штуках — по длине планки
	Смеси и материалы для облицовки							
17	Затирка для швов плитки, класс CG2WA по EN 13888	Mapei Ultracolor Plus 132		Mapei	кг	4,1		по раскладке (a+b)/(a·b) × шов × t × 1,6 + 10 %; в т. ч. 0,1 кг — позиции раскладки без марки
18	Клей плиточный C2 TE S1 по EN 12004, слой 5 мм	Ceresit CM 17		Ceresit	кг	329		14 меш. по 25 кг; 1,5 кг/м² на 1 мм слоя + 10 %; в т. ч. 12 кг — позиции раскладки без марки
19	Гидроизоляция обмазочная мокрых зон: пол, стены по периметру, зоны замачивания; 2 слоя с армирующей лентой в углах	аналог по характеристикам			м²	15,8		площадь по листу раскладки плитки + 10 %; расход смеси — по ТУ
20	Лента демпферная по периметру пола из плитки	аналог по характеристикам			м	26,9		периметр без дверных проёмов + 10 %

Примечания

1. Количества — из геометрии проекта: площади поверхностей по чистым граням стен до отделки (те же, что в ведомости отделки и колерной карте), плитка, клей и затирка — по раскладке плиточника; в графе «Кол.» — к заказу, с запасом.
2. Краска: расход 0,12 л/м² на слой в 2 слоя, если по ТУ не задан иной; запас 10 % и 0,5 л на подкраску каждого кода. Один код — одна партия, колеровка машинная в колеровочном центре бренда; в заказ — только после утверждения выкраса (колерная карта). Фасовка — по каталогу бренда на дату выпуска; к заказу — не меньше расчётного объёма.
3. «Аналог по характеристикам» — допускается изделие другого производителя с характеристиками не ниже указанных, по согласованию с автором проекта.
4. Графы «Код продукции» и «Масса 1 ед.» не заполнены: коды по классификатору продукции не присвоены, масса единицы до 25 кг (ГОСТ 21.110-2013).
5. Грунтовка и клей для доски указаны площадью обработки; объём — по ТУ выбранного продукта.

	Лист	№ док.	Подпись	Дата
Дизайнер	Кырлан А.С.			13.11.26
Проверил				
Н. контр.				
Утв.				

Проект: Квартира 68 м², элитный модерн

Спецификация отделочных материалов

Стадия	Лист	Листов
П	С3	94

выпуск 13.11.2026 № c38d47cb31 · стр. 79 из 94

Список покупок: материалы для магазина

№	Что купить	Артикул или характеристика	Нужно с запасом	Брать в магазине	Фасовка	Уточнить в магазине	Помещения	Кто покупает
Покрытия полов и облицовка								
1	Инженерная доска (дуб натуральный, рабочий слой 4 мм, эмиссия E1, прямая укладка)	по характеристике: инженерная доска, дуб натуральный, масло, 1-полосная, 14/4 мм	52,45 м²	52,5 м²		уточнить в магазине: м² в упаковке	1, 5, 6, 7	по проекту
2	Клей для паркетной и инженерной доски (эластичный, по ТУ изготовителя доски)	на выбор бригады по проекту	49,02 м²			уточнить в магазине: расход и фасовку — по выбранному продукту		бригада
3	Керамогранит 600×600 мм под травертин	по характеристике: керамогранит под травертин	20 шт	21 шт		уточнить в магазине: штук в коробке	2, 3	по проекту
4	Керамогранит 600×1200 мм под травертин	по характеристике: керамогранит под травертин	58 шт	61 шт		уточнить в магазине: штук в коробке	2, 3	по проекту
5	Керамогранит 600×1200 мм ректифицированный под травертин, матовый	по характеристике: керамогранит ректифицированный под травертин, матовый	27 шт	27 шт		уточнить в магазине: штук в коробке	4	по проекту
6	Керамогранит 1200×600 мм под травертин, матовый	по характеристике: керамогранит под травертин, матовый	6 шт	6 шт		уточнить в магазине: штук в коробке	5	по проекту
Сухие смеси и гидроизоляция								
7	Клей плиточный цементный класса C2 TE S1 (ГОСТ Р 56387-2018)	Ceresit CM 17 или аналог	328,77 кг	14 меш.	мешок 25 кг			по проекту
8	Затирка цементная класса CG2WA, цвет — по колерной карте	Mapei Ultracolor Plus 132 или аналог	4,08 кг	3 упак.	упак. 2 кг			по проекту
9	Гидроизоляция обмазочная полимерная, 2 слоя, лента в углах, манжеты на выводах	на выбор бригады по проекту	15,75 м²			уточнить в магазине: расход и фасовку — по выбранному продукту	2, 3	бригада
10	Лента демпферная по периметру пола из плитки	на выбор бригады по проекту	26,85 м	27 м		уточнить в магазине: фасовку		бригада
11	Смесь цементно-песчаная для стяжки М200 (50 мм, 33 мм)	на выбор бригады по проекту	3,53 м³			уточнить в магазине: расход и фасовку — по выбранному продукту		бригада
12	Смесь штукатурная гипсовая для машинного и ручного нанесения по маякам, слой до 10 мм	на выбор бригады по проекту	210,27 м²			уточнить в магазине: расход и фасовку — по выбранному продукту	1, 2, 3, 4, 5, 6, 7	бригада
Короба из ГКЛВ								
13	Лист ГКЛВ 12,5 мм, 2500 × 1200 мм, обшивка коробов в 2 слоя	на выбор бригады по проекту	3,23 м²	2 лист.	лист 3,00 м²		2	бригада
14	Профиль стальной оцинкованный 27 × 28 мм: каркас коробов (стойки и направляющие)	на выбор бригады по проекту	7,7 м	3 шт	хлыст 3 м			бригада
Слаботочные сети								
15	Кабель домофона — тип по системе поставщика	на выбор бригады по проекту	3,1 м	4 м		уточнить в магазине: длину бухты		бригада
16	Кабель коаксиальный RG-6 (75 Ом) к розеткам ТВ	на выбор бригады по проекту	14,1 м	15 м		уточнить в магазине: длину бухты		бригада
17	Кабель U/UTP кат. 5e (LAN, Wi-Fi и камеры по PoE)	на выбор бригады по проекту	27,4 м	28 м		уточнить в магазине: длину бухты		бригада
18	Кабель U/UTP кат. 6 (LAN, Wi-Fi и камеры по PoE)	на выбор бригады по проекту	2,7 м	3 м		уточнить в магазине: длину бухты		бригада
19	Гофротруба Ø20 для слаботочных линий, отдельно от силовых	на выбор бригады по проекту	42,6 м	43 м		уточнить в магазине: длину бухты		бригада
20	Розетка компьютерная RJ45, кат. 6, с рамкой и подрозетником	на выбор бригады по проекту	2 шт	2 шт	шт			бригада
21	Розетка телевизионная (коаксиальная) с рамкой и подрозетником	на выбор бригады по проекту	1 шт	1 шт	шт			бригада
22	Трубка или монитор домофона (поставка домофонной организации)	на выбор бригады по проекту	1 шт	1 шт	шт			по проекту

	Лист	№ док.	Подпись	Дата	Проект: Квартира 68 м², элитный модерн			
Дизайнер	Кырлан А.С.			13.11.26				
Проверил					Список покупок	Стадия	Лист	Листов
Н. контр.						П	С4	94
Утв.								

выпуск 13.11.2026 № c38d47cb31 · стр. 80 из 94

Список покупок: материалы для магазина (продолжение)

№	Что купить	Артикул или характеристика	Нужно с запасом	Брать в магазине	Фасовка	Уточнить в магазине	Помещения	Кто покупает
23	Щит слаботочный ЩС: корпус, DIN-рейка, розетки 220 В	на выбор бригады по проекту	1 шт	1 шт	шт			бригада
24	Патч-панель, портов не менее 3	на выбор бригады по проекту	1 шт	1 шт	шт			бригада
Лакокрасочные материалы								
25	Краска интерьерная акриловая, матовая, класс истирания 1	Tikkurila Euro Power 7, колеровка по NCS No. 30 «Hague Blue глубокий сине-зелёный»	2,53 л	1 банк.	банка 2,7 л		1	по проекту
26	Краска интерьерная акриловая, матовая, класс истирания 1	Farrow & Ball Modern Emulsion No. 2003 «Pointing»	29,55 л	12 банк.	банка 2,5 л		1, 4, 5, 6, 7	по проекту
27	Краска интерьерная акриловая, глубокоматовая, класс истирания 2	Tikkurila Euro Power 7 G503 «Calla»	16,54 л	7 банк.	банка 2,7 л		1, 4, 5, 6, 7	по проекту
28	Краска интерьерная акриловая, матовая, класс истирания 1	Tikkurila Euro Power 7 G503 «Calla»	1,53 л	1 банк.	банка 2,7 л		2, 3	по проекту
29	Краска интерьерная акриловая, матовая, класс истирания 1	Tikkurila Euro Power 7, колеровка по NCS No. 281 «Stiffkey Blue — чернильный синий»	2,63 л	1 банк.	банка 2,7 л		5	по проекту
30	Краска интерьерная акриловая, матовая, класс истирания 1	Farrow & Ball Modern Emulsion No. 43 «Eating Room Red брусничный красный»	2,62 л	2 банк.	банка 2,5 л		6	по проекту
31	Краска интерьерная акриловая, матовая, класс истирания 1	Farrow & Ball Modern Emulsion No. 34 «Calke Green — традиционный шалфей»	3,42 л	2 банк.	банка 2,5 л		7	по проекту
32	Шпаклёвка финишная полимерная под окраску (стены и потолки, Q3)	на выбор бригады по проекту	249,58 м²			уточнить в магазине: расход и фасовку — по выбранному продукту		бригада
33	Грунтовка акриловая глубокого проникновения, 2 слоя	на выбор бригады по проекту	285,58 м²			уточнить в магазине: расход и фасовку — по выбранному продукту		бригада
Погонажные изделия и потолки								
34	Плинтус напольный МДФ под покраску, h=80 мм, крепление к стене	по характеристике: плинтус МДФ под покраску 80×16	70,28 м.п.	30 шт	хлыст 2,4 м		1, 4, 5, 6, 7	по проекту
35	Потолок подвесной ГКЛ/ГКЛВ по каркасу Knauf П113: листы, профили, подвесы, лента, шпаклёвка швов	Knauf П113	68,04 м²		комплект	уточнить в магазине: расход и фасовку — по выбранному продукту		по проекту
Инженерные изделия								
36	Мат нагревательный электрический для тёплого пола под плитку, с холодным концом и муфтой	на выбор бригады по проекту	3 м²			уточнить в магазине: расход и фасовку — по выбранному продукту	3, 4	по проекту
37	Терморегулятор тёплого пола с выносным датчиком пола, монтаж в подрозетник	на выбор бригады по проекту	2 шт	2 шт	шт			по проекту

Примечания

1. «Нужно с запасом» — расход по чертежам и раскладке плюс запас на подрезку и подкраску; «Брать в магазине» — то же количество в единицах, которыми продают (банки, мешки, упаковки, листы, штуки, литры).
2. «Уточнить в магазине» — фасовки этого товара в проекте нет: спросите у продавца, сколько в упаковке, и возьмите целое число упаковок не меньше «Нужно с запасом».
3. Плитку, доску и краску одного цвета берите одной партией (один калибр и тон на помещение) и сохраните чек и номер партии до конца ремонта.
4. «По характеристике» — артикул не выбран: подойдёт любой товар с этими свойствами, согласуйте его с дизайнером до покупки. «Бригада» материал выбирает и закупает бригада по своей технологии.
5. Помещения: 1 — Кабинет; 2 — Санузел; 3 — Ванная; 4 — Прихожая; 5 — Кухня-столовая; 6 — Гостиная; 7 — Спальня; «—» — материал для нескольких помещений, расход по месту.

	Лист	№ док.	Подпись	Дата	Проект: Квартира 68 м², элитный модерн			
Дизайнер	Кырлан А.С.			13.11.26	Список покупок (окончание)	Стадия	Лист	Листов
Проверил						П	С5	94
Н. контр.								
Утв.								

Смета проекта: весь проект по категориям (прайсы собраны 21.09.2026, часть расценок сверена повторно 24.09.2026 и 08.11.2026)

Категория	Позиций	С ценой	По КП	Сумма по позициям с ценой, ₽
Ремонт: работы	55	36	19	991 828
Ремонт: материалы отделки и черновые	32	15	17	654 561
Электрика: кабель, механизмы, щит	37	0	37	
Сантехника: приборы, трубы, арматура	39	0	39	
Доставка и услуги	4	1	3	65 456
Мебель (включая кухню)	21	0	21	
Свет: светильники и ленты	50	0	50	
Техника	7	0	7	
Декор и текстиль	53	0	53	
ИТОГО по позициям с ценой (цены — нижняя граница открытых прайсов)	**298**	**52**	**246**	**1 711 845**
Резерв на непредвиденные работы и материалы, 15 % от ремонта				256 777
ВЕСЬ ПРОЕКТ — вилка «от … до …», ₽				**1 711 845 … 1 968 622**
Позиции «по КП» — цена не названа, в итог НЕ входят: работы — 19; материалы отделки и черновые — 17; электрика: кабель, механизмы, щит — 37; сантехника: приборы, трубы, арматура — 39; доставка и услуги — 3; мебель (включая кухню) — 21; свет: светильники и ленты — 50; техника — 7; декор и текстиль — 53			**246**	**итог выше на их цену**

По этапам

Этап	Поз.	С ценой	Сумма, ₽
Демонтаж и черновые работы (работы)	10	5	248 401
Инженерные системы (работы)	26	14	185 194
Чистовые работы (работы)	19	17	558 233
Черновые материалы (смеси, ГКЛ, гидроизоляция)	12	2	28 200
Электрика: кабель, механизмы, щит, слаботочка	37	0	
Сантехника: приборы, трубы, арматура	39	0	
Чистовые материалы (отделка, двери)	20	13	626 361
Доставка и услуги	4	1	65 456
Резерв на непредвиденное, 15 %	1	1	256 777
Итого ремонт (с резервом)			**1 968 622**

По помещениям

Помещение	Работы, ₽	Материалы, ₽	Всего, ₽
Общее по объекту (без привязки к помещению)	45 434		45 434
1. Кабинет	134 616	74 269	208 885
2. Санузел	73 582	75 638	149 220
3. Ванная	108 479	114 900	223 379
4. Прихожая	151 551	94 737	246 288
5. Кухня-столовая	158 952	99 992	258 944
6. Гостиная	151 039	92 163	243 202
7. Спальня	168 175	102 862	271 037
Доставка и услуги			65 456
Резерв 15 %			256 777
Итого ремонт (с резервом)			**1 968 622**

Работы по этапам с расценками (ориентир)

№	Работа	Ед.	Объём	Расценка, ₽	Сумма, ₽	Расценка	Чей подряд
1. Демонтаж и черновые работы — работы, ориентир по открытым прайсам							
1	Демонтаж существующего покрытия пола до основания	м²	68,47	по КП			бригада
2	Демонтаж существующей отделки стен до основания	м²	191,15	по КП			бригада
3	Демонтаж существующей отделки потолка до основания	м²	68,47	по КП			бригада

	Лист	№ док.	Подпись	Дата	Проект: Квартира 68 м², элитный модерн			
Дизайнер	Кырлан А.С.			13.11.26	Смета проекта: этапы, помещения, итог	Стадия	Лист	Листов
Проверил						П	С6	94
Н. контр.								
Утв.								

выпуск 13.11.2026 № c38d47cb31 · стр. 82 из 94

Работы по этапам с расценками (ориентир) (продолжение)

№	Работа	Ед.	Объём	Расценка, ₽	Сумма, ₽	Расценка	Чей подряд
4	Демонтаж существующих дверных блоков	шт	7,00	по КП			бригада
5	Демонтаж существующих сантехприборов и электрооборудования (если есть)	компл		по КП			бригада
6	Устройство стяжки: стяжка ЦПС М200, 50 мм	м²	69,26	530	36 708	Ц1	бригада
7	Гидроизоляция обмазочная, 2 слоя: пол, стены на 200 мм, зоны замачивания	м²	14,32	450	6 444	Ц1	бригада
8	Штукатурка стен по маякам, до 10 мм	м²	191,15	530	101 310	Ц1	бригада
9	Штукатурка оконных откосов шириной до 200 мм	м²	3,48	540	1 879	Ц4	бригада
10	Потолок ГКЛ по каркасу П113, 1 слой	м²	68,04	1 500	102 060	Ц1	бригада
2. Инженерные системы — работы, ориентир по открытым прайсам							
11	Прокладка кабеля ВВГнг(А)-LS по группам щита: за потолком и в штробах стен (штробы — только после технического заключения, см. строку «Штробы в стенах»)	м	571,00	60	34 260	Ц3	бригада
12	Прокладка слаботочной линии: Кабель домофона — тип по системе поставщика, отдельно от силовых	м	3,10	по КП			бригада
13	Прокладка слаботочной линии: Кабель коаксиальный RG-6 (75 Ом) к розеткам ТВ, отдельно от силовых	м	14,10	по КП			бригада
14	Прокладка слаботочной линии: Кабель U/UTP кат. 5e (LAN, Wi-Fi и камеры по PoE), отдельно от силовых	м	27,40	по КП			бригада
15	Прокладка слаботочной линии: Кабель U/UTP кат. 6 (LAN, Wi-Fi и камеры по PoE), отдельно от силовых	м	2,70	по КП			бригада
16	Прокладка гофротрубы Ø20 для слаботочных линий, отдельно от силовых	м	42,60	140	5 964	Ц3	бригада
17	Сборка слаботочного щита ЩС: корпус, патч-панель, подключение линий и питания 220 В; коммутатор и точки доступа — оборудование заказчика	шт	1,00	по КП			бригада
18	Электроточка: подрозетник в бетоне, розетка, выключатель, вывод	шт	73,00	950	69 350	Ц3	бригада
19	Штробы в стенах под спуски кабеля к точкам — выполняются только после технического заключения о несущих стенах	м	119,19	по КП			бригада
20	Установка встраиваемого точечного светильника	шт	42,00	750	31 500	Ц3	бригада
21	Монтаж светильника: потолочного, подвесного, настенного	шт	7,00	1 200	8 400	Ц3	бригада
22	Монтаж LED-ленты в алюминиевый профиль	м	3,00	230	690	Ц3	бригада
23	Установка блока питания LED в доступном месте (люк, шкаф)	шт	1,00	570	570	Ц3	бригада
24	Установка автономного пожарного извещателя	шт	5,00	по КП			бригада
25	Сборка щита: установка автоматов и АВДТ групп, вводного автомата	шт	21,00	230	4 830	Ц3	бригада
26	Установка вводного УЗО	шт	1,00	380	380	Ц3	бригада
27	Монтаж инсталляции, установка подвесного унитаза и кнопки смыва	шт	1,00	10 500	10 500	Ц1	бригада
28	Короб инсталляции: каркас и обшивка ГКЛВ в 2 слоя, ревизионный доступ к смыву	шт	2,00	по КП			бригада
29	Короб К1 над чистым полом: каркас и обшивка ГКЛВ под плитку (материалы — в спецификации ВК)	м	2,07	по КП			бригада
30	Установка ванны с сифоном	шт	1,00	6 000	6 000	Ц1	бригада
31	Установка умывальника (мойки) с сифоном и смесителем	шт	3,00	3 000	9 000	Ц1	бригада
32	Подключение стиральной (посудомоечной) машины к ВК	шт	2,00	по КП			бригада
33	Установка радиатора с узлом подключения и терморегулятором	шт	4,00	по КП			бригада
34	Монтаж сплит-системы КВ-1: внутренний блок на стене, трасса фреона и дренажа до наружного блока, вакуумирование, пусконаладка	шт	2,00	по КП			бригада
35	Электрический тёплый пол: укладка нагревательного мата в слой клея, датчик пола в гофротрубе	м²	3,00	750	2 250	Ц1	бригада
36	Установка терморегулятора тёплого пола с датчиком в гофротрубе	шт	2,00	750	1 500	Ц1	бригада

	Лист	№ док.	Подпись	Дата	Проект: Квартира 68 м², элитный модерн			
Дизайнер	Кырлан А.С.			13.11.26	Смета проекта: этапы, помещения, итог (продолжение)	Стадия	Лист	Листов
Проверил						П	С7	94
Н. контр.								
Утв.								

выпуск 13.11.2026 № c38d47cb31 · стр. 83 из 94

Работы по этапам с расценками (ориентир) (продолжение)

№	Работа	Ед.	Объём	Расценка, ₽	Сумма, ₽	Расценка	Чей подряд
3. Чистовые работы — работы, ориентир по открытым прайсам							
37	Облицовка стен керамогранитом 600×1200 на клею	м²	28,76	2 500	71 900	Ц5	бригада
38	Облицовка короба инсталляции (ГКЛВ) керамогранитом: лицо, боковины, полка	м²	1,47	2 500	3 675	Ц5	бригада
39	Облицовка фартука керамогранитом 1200×600	м²	1,68	2 400	4 032	Ц2	бригада
40	Укладка керамогранита на пол, 600×600, на клею	м²	20,23	1 800	36 414	Ц2	бригада
41	Затирка швов керамогранита	м²	51,59	150	7 739	Ц2	бригада
42	Грунтование стен, 2 слоя (под штукатурку и под отделку)	м²	191,15	96	18 350	Ц4	бригада
43	Шпаклёвка стен под окраску, 2 слоя (старт и финиш), уровень Q3	м²	158,42	750	118 815	Ц1	бригада
44	Грунтование и шпаклёвка оконных откосов, 2 слоя	м	18,28	300	5 484	Ц4	бригада
45	Грунтование потолка, 2 слоя	м²	68,47	96	6 573	Ц4	бригада
46	Шпаклёвка потолка под окраску, 2 слоя, уровень Q3	м²	68,47	950	65 047	Ц1	бригада
47	Окраска потолка водно-дисперсионной краской, 2 слоя	м²	68,47	360	24 649	Ц1	бригада
48	Окраска стен водно-дисперсионной краской, 2 слоя	м²	183,69	300	55 107	Ц1	бригада
49	Окраска оконных откосов, 2 слоя	м	18,28	120	2 194	Ц4	бригада
50	Укладка инженерной доски на клей	м²	49,03	1 200	58 836	Ц1	бригада
51	Установка плинтуса МДФ h=80 мм	м	63,89	450	28 751	Ц1	бригада
52	Окраска плинтуса в тоне No. 2003, 2 слоя	м	63,89	300	19 167	Ц1	бригада
53	Монтаж межкомнатных дверей (поставщик дверей)	шт	6,00	5 250	31 500	Ц1	поставщик
54	Входная дверь, поставка с монтажом и откосами	шт	1,00	по КП			поставщик
55	Монтаж телевизора ОБ-03 на кронштейн, скрытая прокладка HDMI и питания (штроба, трубка), подключение акустики	шт	1,00	по КП			бригада
4. Прочие работы и услуги — работы, ориентир по открытым прайсам							
56	Кухонный гарнитур по проекту кухни, изготовление и монтаж (4–8 нед.)	компл	1,00	по КП			поставщик
	Итого работы (позиции с расценкой)				**991 828**		

Примечания

1. Итог «ВЕСЬ ПРОЕКТ» — не прогноз, а сумма того, у чего есть цена: ремонт (работы и материалы по смете сметчика), мебель, свет, техника и декор — по ценам из данных проекта. Позиции без цены названы «по КП» (246 шт.) и в итог не входят: пока цена не названа, итог выше напечатанного.
2. Вилка: «от» — сумма по позициям с ценой по нижней границе открытых прайсов (прайсы собраны 21.09.2026, часть расценок сверена повторно 24.09.2026 и 08.11.2026, Москва); «до» — «от» плюс резерв на непредвиденное (15 % от ремонта; частный ремонт 10–20 %).
3. Работы — ориентир по прайсам подрядчиков, не договорная цена: расценку называет бригада после контрольного обмера. Материалы — по «Смете материалов с ценами» (следующий лист).
4. Разбивка по помещениям — доли: общая закупка делится пропорционально площади (длине, числу), по которой считается позиция; работы — по объёму строки в помещении. Сумма по помещениям, по этапам и по категориям одна и та же.
5. Источники расценок и цен: Ц1 — Домашний мастерок: прайс на отделочные работы, 2026; Ц2 — Домашний мастерок: прайс на плиточные работы, 2026; Ц3 — Домашний мастерок: прайс на электромонтажные работы, 2026; Ц4 — Профи ремонтник: штукатурно-малярные работы; Ц5 — Profi.ru: укладка керамогранита на стены, Москва 2026; Ц6 — справочник материалов: ориентир по сегментам; Ц7 — Розница Москвы, 09.2026: Лемана ПРО, KGSnab, официальный дилер Farrow & Ball.
6. Оборудование «по КП» из сметы сметчика (кухня и др.): 1 поз. — в позиции «по КП» мебели и техники.

	Лист	№ док.	Подпись	Дата	Проект: Квартира 68 м², элитный модерн			
Дизайнер	Кырлан А.С.			13.11.26	Смета проекта: этапы, помещения, итог (окончание)	Стадия	Лист	Листов
Проверил						П	С8	94
Н. контр.								
Утв.								

выпуск 13.11.2026 № c38d47cb31 · стр. 84 из 94

Смета материалов с ценами

№	Позиция	Ед.	Нетто	Запас	С запасом	К закупке (упаковка)	Цена за ед., ₽	Сумма, ₽	Заказать заранее	Доп.
Чистовая отделка — позиций 20, с ценой 13, итого 626 361 ₽										
Покрытия полов и облицовка										
1	Инженерная доска (дуб натуральный, рабочий слой 4 мм, эмиссия E1, прямая укладка)	м²	49,02	7 %	52,45	52,50 м²	4 513 / м²	236 933		1, 7
2	Керамогранит 600×600 мм под травертин — керамогранит под травертин	шт	18	17 %	21	21 шт · коробка	1 800 / м²	13 608		1, 7
3	Керамогранит 600×1200 мм под травертин — керамогранит под травертин	шт	52	17 %	61	61 шт · коробка	3 500 / м²	153 720		1, 7
4	Керамогранит 600×1200 мм ректифицированный под травертин, матовый — керамогранит ректифицированный под травертин, матовый	шт	24	13 %	27	27 шт · коробка	3 500 / м²	68 040		1, 7
5	Керамогранит 1200×600 мм под травертин, матовый — керамогранит под травертин, матовый	шт	5	20 %	6	6 шт · коробка	3 500 / м²	15 120		1, 7
Лакокрасочные материалы										
6	Краска интерьерная акриловая, матовая, класс истирания 1 — Tikkurila Euro Power 7, колеровка по NCS No. 30 «Hague Blue — глубокий сине-зелёный»	л	2,30	10 %	2,53	1 банка · банка 2,7 л	3 510 / банк	3 510		7
7	Краска интерьерная акриловая, матовая, класс истирания 1 — Farrow & Ball Modern Emulsion No. 2003 «Pointing»	л	26,86	10 %	29,55	12 банка · банка 2,5 л	5 800 / банк	69 600		7
8	Краска интерьерная акриловая, глубокоматовая, класс истирания 2 — Tikkurila Euro Power 7 G503 «Calla»	л	15,04	10 %	16,54	7 банка · банка 2,7 л	3 510 / банк	24 570		7
9	Краска интерьерная акриловая, матовая, класс истирания 1 — Tikkurila Euro Power 7 G503 «Calla»	л	1,39	10 %	1,53	1 банка · банка 2,7 л	3 510 / банк	3 510		7
10	Краска интерьерная акриловая, матовая, класс истирания 1 — Tikkurila Euro Power 7, колеровка по NCS No. 281 «Stiffkey Blue — чернильный синий»	л	2,39	10 %	2,63	1 банка · банка 2,7 л	3 510 / банк	3 510		7
11	Краска интерьерная акриловая, матовая, класс истирания 1 — Farrow & Ball Modern Emulsion No. 43 «Eating Room Red — брусничный красный»	л	2,38	10 %	2,62	2 банка · банка 2,5 л	5 800 / банк	11 600		7
12	Краска интерьерная акриловая, матовая, класс истирания 1 — Farrow & Ball Modern Emulsion No. 34 «Calke Green — традиционный шалфей»	л	3,11	10 %	3,42	2 банка · банка 2,5 л	5 800 / банк	11 600		7
Погонажные изделия и потолки										
13	Плинтус напольный МДФ под покраску, h=80 мм, крепление к стене — плинтус МДФ под покраску 80×16	м	63,89	10 %	70,28	30 шт · хлыст 2,4 м	368 / шт	11 040		1, 7
Двери										
14	Дверь межкомнатная Д-1, проём 880×2100 мм	шт	1		1	1 шт	по запросу			6
15	Дверь межкомнатная Д-2, проём 790×2100 мм	шт	1		1	1 шт	по запросу			6
16	Дверь межкомнатная Д-3, проём 790×2100 мм	шт	1		1	1 шт	по запросу			6
17	Дверь межкомнатная Д-4, проём 880×2100 мм	шт	1		1	1 шт	по запросу			6
18	Дверь межкомнатная Д-5, проём 880×2100 мм	шт	1		1	1 шт	по запросу			6
19	Дверь входная Д-6, проём 880×2100 мм	шт	1		1	1 шт	по запросу			6
20	Дверь межкомнатная Д-7, проём 880×2100 мм	шт	1		1	1 шт	по запросу			6
Черновые материалы — позиций 12, с ценой 2, итого 28 200 ₽										
Покрытия полов и облицовка										
21	Клей для паркетной и инженерной доски (эластичный, по ТУ изготовителя доски)	м²	49,02		49,02	фасовка по ТУ изделия	по запросу			2
Сухие смеси и гидроизоляция										
22	Клей плиточный цементный класса C2 TE S1 (ГОСТ Р 56387-2018) — Ceresit CM 17 или аналог	кг	298,88	10 %	328,77	14 мешок · мешок 25 кг	1 800 / меш.	25 200		7
23	Затирка цементная класса CG2WA, цвет — по колерной карте — Mapei Ultracolor Plus 132 или аналог	кг	3,71	10 %	4,08	3 упаковка · упак. 2 кг	1 000 / упак.	3 000		7
24	Гидроизоляция обмазочная полимерная, 2 слоя, лента в углах, манжеты на выводах	м²	14,32	10 %	15,75	фасовка по ТУ изделия	по запросу			2
25	Лента демпферная по периметру пола из плитки	м	24,41	10 %	26,85	27,00 м	по запросу			
26	Смесь цементно-песчаная для стяжки М200 (50 мм, 33 мм)	м³	3,36	5 %	3,53	фасовка по ТУ изделия	по запросу			2
27	Смесь штукатурная гипсовая для машинного и ручного нанесения по маякам, слой до 10 мм	м²	191,15	10 %	210,27	фасовка по ТУ изделия	по запросу			2

	Лист	№ док.	Подпись	Дата	Проект: Квартира 68 м², элитный модерн			
Дизайнер	Кырлан А.С.			13.11.26				
Проверил					Смета материалов с ценами	Стадия	Лист	Листов
Н. контр.						П	С9	94
Утв.								

выпуск 13.11.2026 № c38d47cb31 · стр. 85 из 94

Смета материалов с ценами (продолжение)

№	Позиция	Ед.	Нетто	Запас	С запасом	К закупке (упаковка)	Цена за ед., ₽	Сумма, ₽	Заказать заранее	Доп.
Короба из ГКЛВ										
28	Лист ГКЛВ 12,5 мм, 2500 × 1200 мм, обшивка коробов в 2 слоя	м²	2,94	10 %	3,23	2 лист · лист 3,00 м²	по запросу			
29	Профиль стальной оцинкованный 27 × 28 мм: каркас коробов (стойки и направляющие)	м	7,00	10 %	7,70	3 шт · хлыст 3 м	по запросу			
Лакокрасочные материалы										
30	Шпаклёвка финишная полимерная под окраску (стены и потолки, Q3)	м²	226,89	10 %	249,58	фасовка по ТУ изделия	по запросу			2
31	Грунтовка акриловая глубокого проникновения, 2 слоя	м²	259,62	10 %	285,58	фасовка по ТУ изделия	по запросу			2
Погонажные изделия и потолки										
32	Потолок подвесной ГКЛ/ГКЛВ по каркасу Knauf П113: листы, профили, подвесы, лента, шпаклёвка швов	м²	68,04		68,04	фасовка по ТУ изделия	по запросу			2
Электрика и слаботочные сети — позиций 37, с ценой 0, итого 0 ₽										
Слаботочные сети										
33	Кабель домофона — тип по системе поставщика	м	3,10		3,10	4,00 м	по запросу			3
34	Кабель коаксиальный RG-6 (75 Ом) к розеткам ТВ	м	14,10		14,10	15,00 м	по запросу			3
35	Кабель U/UTP кат. 5e (LAN, Wi-Fi и камеры по PoE)	м	27,40		27,40	28,00 м	по запросу			3
36	Кабель U/UTP кат. 6 (LAN, Wi-Fi и камеры по PoE)	м	2,70		2,70	3,00 м	по запросу			3
37	Гофротруба Ø20 для слаботочных линий, отдельно от силовых	м	42,60		42,60	43,00 м	по запросу			3
38	Розетка компьютерная RJ45, кат. 6, с рамкой и подрозетником	шт	2		2	2 шт	по запросу			
39	Розетка телевизионная (коаксиальная) с рамкой и подрозетником	шт	1		1	1 шт	по запросу			
40	Трубка или монитор домофона (поставка домофонной организации)	шт	1		1	1 шт	по запросу			
41	Щит слаботочный ЩС: корпус, DIN-рейка, розетки 220 В	шт	1		1	1 шт	по запросу			
42	Патч-панель, портов не менее 3	шт	1		1	1 шт	по запросу			
Инженерные изделия										
43	Мат нагревательный электрический для тёплого пола под плитку, с холодным концом и муфтой	м²	3,00		3,00	фасовка по ТУ изделия	по запросу			2
44	Терморегулятор тёплого пола с выносным датчиком пола, монтаж в подрозетник	шт	2		2	2 шт	по запросу			
Электрика: силовая часть										
45	Кабель силовой ВВГнг(А)-LS 3×1,5 мм²	м	145,00		145,00	145,00 м	по запросу			3
46	Кабель силовой ВВГнг(А)-LS 3×2,5 мм²	м	408,00		408,00	408,00 м	по запросу			3
47	Кабель силовой ВВГнг(А)-LS 3×6 мм²	м	18,00		18,00	18,00 м	по запросу			3
Электрика: щит										
48	Автоматический выключатель дифференциального тока (АВДТ) C10 A, 30 мА, тип A	шт	4		4	4 шт	по запросу			4
49	Автоматический выключатель дифференциального тока (АВДТ) C16 A, 30 мА, тип A	шт	15		15	15 шт	по запросу			4
50	Автоматический выключатель дифференциального тока (АВДТ) C32 A, 30 мА, тип A	шт	1		1	1 шт	по запросу			4
51	Корпус щита ЩРВ-П-72, IP41, 72 модулей	шт	1		1	1 шт	по запросу			4
52	Вводной автомат C50, 1P+N	шт	1		1	1 шт	по запросу			4
53	Вводное УЗО-S 63 A, 100 мА (селективное)	шт	1		1	1 шт	по запросу			4
54	УЗИП тип 2	шт	1		1	1 шт	по запросу			4
Электрика: механизмы и изделия										

	Лист	№ док.	Подпись	Дата
Дизайнер	Кырлан А.С.			13.11.26
Проверил				
Н. контр.				
Утв.				

Проект: Квартира 68 м², элитный модерн

Смета материалов с ценами (продолжение)	Стадия	Лист	Листов
	П	С10	94

Смета материалов с ценами (продолжение)

№	Позиция	Ед.	Нетто	Запас	С запасом	К закупке (упаковка)	Цена за ед., ₽	Сумма, ₽	Заказать заранее	Доп.
55	Розетка с з/к и защитными шторками, 16 А	шт	53		53	53 шт	по запросу			4
56	Розетка IP44 с крышкой, 16 А	шт	3		3	3 шт	по запросу			4
57	Выключатель 1-клав.	шт	3		3	3 шт	по запросу			4
58	Выключатель 1-клав. проходной	шт	1		1	1 шт	по запросу			4
59	Выключатель 2-клав.	шт	5		5	5 шт	по запросу			4
60	Выключатель 2-клав. (перекрёстная + проходная)	шт	1		1	1 шт	по запросу			4
61	Выключатель 2-клав. проходной	шт	1		1	1 шт	по запросу			4
62	Рамка 1-постовая	шт	43		43	43 шт	по запросу			4
63	Рамка 2-постовая	шт	12		12	12 шт	по запросу			4
64	Терморегулятор тёплого пола	шт	2		2	2 шт	по запросу			4
65	Коробка установочная (подрозетник) Ø68	шт	69		69	69 шт	по запросу			4
66	Вывод кабеля под прибор (клеммник)	шт	13		13	13 шт	по запросу			4
67	Коробка уравнивания потенциалов КУП	шт	2		2	2 шт	по запросу			4
68	Извещатель дымовой автономный	шт	3		3	3 шт	по запросу			4
69	Извещатель тепловой	шт	2		2	2 шт	по запросу			4
Сантехника — позиций 39, с ценой 0, итого 0 ₽										
Сантехника: санитарные приборы										
70	Ванна встраиваемая акриловая 1700×750 мм, с каркасом, экраном и отверстием слив-перелив — акриловая 1700×750, смеситель настенный	шт	1		1	1 шт	по запросу			5
71	Унитаз подвесной безободковый, с сиденьем микролифт, крепёж и звукоизолирующая прокладка — инсталляция 1120 + подвесной унитаз	шт	1		1	1 шт	по запросу			5
72	Инсталляция для подвесного унитаза: рама высотой 1120 мм, бачок, клавиша смыва (ось клавиши 1050 мм от чистого пола)	шт	1		1	1 шт	по запросу			5, 1
73	Умывальник подвесной 400×280 мм, с отверстием под смеситель и переливом — раковина подвесная 400 × 280, смеситель на раковине — аналог по характеристикам	шт	1		1	1 шт	по запросу			5
74	Раковина накладная 800×500 мм, на столешницу тумбы, с переливом — раковина-столешница на подвесной тумбе 800 × 500, смеситель на раковине — аналог по характеристикам	шт	1		1	1 шт	по запросу			5
75	Гигиенический душ: ручная лейка с кнопкой-запорником, шланг 1,25 м, настенный держатель	шт	1		1	1 шт	по запросу			5, 1
76	Мойка врезная, нержавеющая сталь 700×480 мм, с переливом	шт	1		1	1 шт	по запросу			5, 1
77	Фильтр обратного осмоса под мойку, с отдельным краном и врезкой дренажа	шт	1		1	1 шт	по запросу			5, 1
Сантехника: смесители, сифоны и арматура приборов										
78	Смеситель для ванны настенный однорычажный, межосевое 150 мм, с душевым набором (лейка, шланг, держатель)	шт	1		1	1 шт	по запросу			5, 1
79	Смеситель для умывальника однорычажный, с донным клапаном	шт	1		1	1 шт	по запросу			5, 1
80	Смеситель для накладной раковины однорычажный, высокий излив, с донным клапаном	шт	1		1	1 шт	по запросу			5, 1
81	Смеситель кухонный однорычажный, высокий излив	шт	1		1	1 шт	по запросу			5, 1
82	Смеситель для гигиенического душа скрытого монтажа однорычажный: встраиваемая часть, накладная панель с рычагом, вывод на лейку; встраиваемая часть — до плитки	шт	1		1	1 шт	по запросу			5, 1
83	Обвязка ванны слив-перелив Ø40/50 с сифоном	шт	1		1	1 шт	по запросу			5, 1
84	Сифон для умывальника бутылочный Ø32/40–50, с гофрой к выпуску	шт	2		2	2 шт	по запросу			5, 1
85	Сифон для мойки Ø40/50	шт	1		1	1 шт	по запросу			5, 1
86	Сифон для посудомоечной машины с обратным клапаном, на выводе слива Ø40	шт	1		1	1 шт	по запросу			5, 1

	Лист	№ док.	Подпись	Дата	Проект: Квартира 68 м², элитный модерн			
Дизайнер	Кырлан А.С.			13.11.26	Смета материалов с ценами (продолжение)	Стадия	Лист	Листов
Проверил						П	С11	94
Н. контр.								
Утв.								

выпуск 13.11.2026 № c38d47cb31 · стр. 87 из 94

Смета материалов с ценами (продолжение)

№	Позиция	Ед.	Нетто	Запас	С запасом	К закупке (упаковка)	Цена за ед., ₽	Сумма, ₽	Заказать заранее	Доп.
87	Сифон для стиральной машины встраиваемый в стену Ø50, с обратным клапаном	шт	1		1	1 шт	по запросу			5, 1
88	Кран угловой ½"×½" с гибкой подводкой 40 см (умывальники, мойка)	шт	6		6	6 шт	по запросу			5, 1
89	Кран шаровой угловой ½"×¾" для подключения стиральной и посудомоечной машины	шт	2		2	2 шт	по запросу			5, 1
Сантехника: трубопроводы										
90	Труба полипропиленовая PP-R PN20 Ø20×3,4 (B1) — ГОСТ 32415-2013	м	17,50	10 %	17,50	17,50 м	по запросу			5
91	Труба PP-R, армированная стекловолокном, PN20 Ø20×2,8 (Т3) — ГОСТ 32415-2013	м	14,00	10 %	14,00	14,00 м	по запросу			5
92	Труба канализационная ПП Ø40 (К1) — ГОСТ 32414-2013	м	6,50	10 %	6,50	6,50 м	по запросу			5
93	Труба канализационная ПП Ø50 (К1) — ГОСТ 32414-2013	м	8,00	10 %	8,00	8,00 м	по запросу			5
94	Труба канализационная ПП Ø110 (К1) — ГОСТ 32414-2013	м	2,00	10 %	2,00	2,00 м	по запросу			5
Сантехника: фасонные части и выводы										
95	Отвод канализационный ПП 45° Ø40 — ГОСТ 32414-2013	шт	10		10	10 шт	по запросу			5
96	Отвод канализационный ПП 45° Ø50 — ГОСТ 32414-2013	шт	12		12	12 шт	по запросу			5
97	Отвод канализационный ПП 45° Ø110 — ГОСТ 32414-2013	шт	6		6	6 шт	по запросу			5
98	Тройник канализационный ПП 45° (врезки ветвей) — ГОСТ 32414-2013	шт	7		7	7 шт	по запросу			5
99	Ревизия канализационная ПП (после поворота трассы) — ГОСТ 32414-2013	шт	8		8	8 шт	по запросу			5
100	Фитинги PP-R Ø20: тройники, угольники 90° (ветви и повороты В1, Т3) — ГОСТ 32415-2013	шт	23		23	23 шт	по запросу			5
101	Водорозетка PP-R Ø20×½" настенная, с креплением — ГОСТ 32415-2013	шт	14		14	14 шт	по запросу			5
Сантехника: узлы ввода, люки, короба										
102	Кран шаровой латунный Ду15 PN16 (отключение ввода)	шт	2		2	2 шт	по запросу			5, 1
103	Фильтр сетчатый косой Ду15	шт	2		2	2 шт	по запросу			5, 1
104	Счётчик воды крыльчатый Ду15 (ХВ, ГВ), с поверкой	шт	2		2	2 шт	по запросу			5, 1
105	Клапан обратный Ду15	шт	2		2	2 шт	по запросу			5, 1
106	Люк ревизионный нажимной под плитку 300×400 мм	шт	4		4	4 шт	по запросу			5, 1
107	Звукоизоляция стояка К1 в коробе: рулонный звукоизоляционный материал ≥ 10 мм, обмотка стояка на высоту этажа	м	2,70		2,70	2,70 м	по запросу			5, 1
108	Короб К1 над полом: профиль ПН/ПС, ГКЛВ 12,5 мм под плитку	м	2,30		2,30	2,30 м	по запросу			5, 1
	ИТОГО материалы (позиций с ценой 15 из 108; без цены 93 — «по запросу», в итог не входят)							**654 561**		

Примечания

1. Количества — из единой книги материалов проекта: тот же расход, что в спецификации отделочных материалов, смете и списке покупок. Запас — на подрезку и бой; норма запаса печатается в графе «Запас», её основание — в отдельном документе «Смета на материалы».
2. Цены — нижняя граница открытых прайсов (прайсы собраны 21.09.2026, часть расценок сверена повторно 24.09.2026 и 08.11.2026, Москва); не предложение (оферта) магазинов. Цены нет — «по запросу», позиция в итог не входит. Работы в эту смету не входят (они — на листе «Смета проекта»).
3. Доп. 1. Изделие не выбрано: позиция описана по характеристикам («аналог»); марка, артикул и цена определяются при выборе изделия.
4. Доп. 2. Фасовка не задана в данных: количество дано в мерах расчёта, число упаковок определяется по выбранному продукту (расход и тара — по ТУ).
5. Доп. 3. Длина кабеля — по длинам групп щита из данных электрика; запас на подрезку в длину не заложен — берите бухту с запасом 5–10 %.
6. Доп. 4. Механизмы, рамки и подрозетники — по ведомости изделий электрика; серию механизмов выбирает заказчик.
7. Доп. 5. Трубы и фасонные части — по трассам листа разводки, +10 % на подрезку (уже в количестве); модели приборов заказчик выбирает сам.
8. Доп. 6. Двери: цена и срок называет поставщик после выбора изделия; в смету стоят только если цена задана в данных.
9. Доп. 7. Цена — нижняя граница открытых прайс-листов на дату сбора (книга цен проекта); не коммерческое предложение магазина.
10. Доп. 8. Доли по помещениям справочные: общая закупка делится пропорционально площади (длине, числу), по которой считается позиция.

	Лист	№ док.	Подпись	Дата
Дизайнер	Кырлан А.С.			13.11.26
Проверил				
Н. контр.				
Утв.				


Проект: Квартира 68 м², элитный модерн

Смета материалов с ценами (окончание)	Стадия	Лист	Листов
	П	С12	94

выпуск 13.11.2026 № c38d47cb31 · стр. 88 из 94

1 Порог 15 мм: мокрая зона — смежное помещение (М 1:5)


Применение: двери Д-2, Д-3

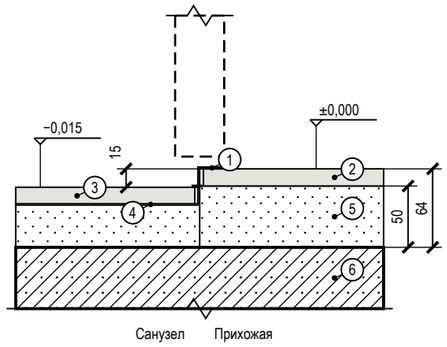

Поз.	Состав слоя, изделие
1	порог-переход металлический, перепад 15 мм, на клей-герметик
2	керамогранит на клею C2 TE S1
3	керамогранит на клею C2 TE S1
4	гидроизоляция в 2 слоя с подъёмом на торец ступени, лента в углу
5	ЦПС М200 50 мм; в мокрой зоне 33 мм
6	плита перекрытия

2 Короб стояков К1-1 с люком и звукоизоляцией (М 1:20)


Применение: пом. 3

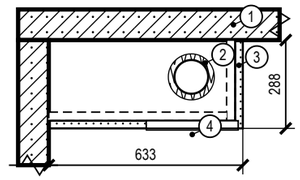

Поз.	Состав слоя, изделие
1	стены существующие — не ослаблять
2	звукоизоляция стояков рулонная 20 мм; К1-1 Ø110
3	короб: профиль 27×28, ГКЛВ 2×12,5 мм, облицовка плиткой
4	ревизионный люк 300×400 мм нажимной, под плитку; против ревизии стояка

3 Гидроизоляция санузла: заход на стены 200 мм, примыкание ванны (М 1:20)


Применение: пом. 2, 3

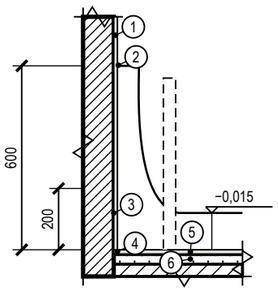

Поз.	Состав слоя, изделие
1	облицовка — плитка на клею C2 TE S1, затирка CG2WA
2	примыкание ванны: лента бордюрная + силиконовый санитарный герметик; облицовка опирается на борт
3	гидроизоляция обмазочная в 2 слоя, заход на стены 200 мм (в зоне душа — выше), до облицовки; акт скрытых работ, тест проливом
4	лента гидроизоляционная в углах и у трапов
5	керамогранит на клею C2 TE S1
6	ЦПС М200 33 мм

4 Плинтус МДФ 80×16 мм у окрашенной стены по доске (ламинату) (М 1:10)


Применение: пом. 1, 5, 6, 7

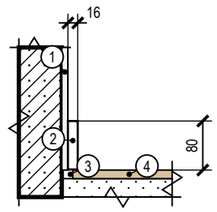

Поз.	Состав слоя, изделие
1	штукатурка, шпаклёвка Q3, окраска — по ведомости отделки
2	плинтус МДФ 80×16 под окраску в цвет стены; клей монтажный — к стене, не к полу
3	зазор покрытия у стены 8–10 мм закрывается плинтусом
4	инженерная доска на клею

5 Плинтус МДФ 80×16 мм у окрашенной стены по керамограниту (плитке) (М 1:10)

Применение: пом. 4

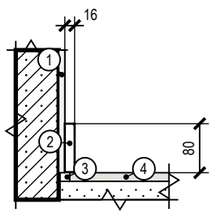

Поз.	Состав слоя, изделие
1	штукатурка, шпаклёвка Q3, окраска — по ведомости отделки
2	плинтус МДФ 80×16 под окраску в цвет стены; клей монтажный — к стене, не к полу
3	зазор покрытия у стены 8–10 мм закрывается плинтусом
4	керамогранит на клею C2 TE S1

Условные обозначения

- железобетон (плита, стены) — условно: конструкция не установлена
- кладка, перегородка — условно: конструкция не установлена
- стяжка, раствор
- гипсокартон ГКЛВ
- звукоизоляция, эластичный заполнитель
- плитка, керамогранит на клею
- инженерная доска (покрытие пола)
- металлический профиль (порог, Т-профиль, короб двери)
- гидроизоляция (обмазочная, лента)


Примечания

1. Узлы — типовые решения проекта для мест, отмеченных выносками на листе схемы расположения развёрток и узлов; размеры — в мм, отметки — в м от ±0,000.
2. Узлы с гидроизоляцией, закладными и коробами скрытого монтажа принимаются по актам скрытых работ до закрытия отделкой; гидроизоляция — после теста проливом (24 ч).
3. Марки изделий (порог, Т-профиль, короб скрытой двери, люк) — по спецификациям; замена — на аналог с теми же габаритами по согласованию с автором проекта.
4. Материал плиты перекрытия и стен в узлах показан условно (железобетон, кладка): конструкция дома не установлена — крепёж, анкеры и толщины слоёв уточняются после обследования (до него — по допущениям общих указаний).

	Лист	№ док.	Подпись	Дата	Проект: Квартира 68 м², элитный модерн			
Дизайнер	Кырлан А.С.			13.11.26	Узлы	Стадия	Лист	Листов
Проверил						П	С13	94
Н. контр.								
Утв.								

выпуск 13.11.2026 № c38d47cb31 · стр. 89 из 94

№	Работа	Нед.	После
Р-1	**демонтаж**	1	
Р-2	**контрольный обмер**	0,5	Р-1
Р-3	**черновая электрика**	1,5	Р-2
Р-4	черновая сантехника	1	Р-2
Р-5	**штукатурка**	2,25	Р-3, Р-4
Р-6	**стяжка**	0,75	Р-5
Р-7	**гидроизоляция**	0,5	Р-6
Р-8	ГКЛ	1,5	Р-3, Р-4
Р-9	**плитка**	3	Р-7, Р-8, Р-6
Р-10	**шпаклёвка**	2,75	Р-9, Р-8, Р-5
Р-11	**окраска**	2	Р-10
Р-12	**чистовые полы**	1	Р-11, Р-9
Р-13	**двери и плинтусы**	0,75	Р-12, Р-11
Р-14	**чистовая электрика и сантехника**	1	Р-13, Р-11
Р-15	**кухня и мебель**	1	Р-14, Р-13
Р-16	**сдача**	0,75	Р-15, Р-14
Закупки: заказать не позднее — «◆»; от заказа до поставки — штриховая полоса; срок поставки — только из данных или «ориентир практики»			
З-1	Кухонный гарнитур по проекту кухни: модули М-06, М-07, М-08, М-09, М-10, М-11, М-13, М-14,	6	для Р-15
З-2	Встраиваемая техника кухни: М-06 холодильник, М-08 духовой шкаф, М-11 посудомоечная машина, М-14 в		для Р-15
З-3	Стиральная машина: ОБ-01 (вертикальная загрузка 400 × 600 мм — условие закупки)		для Р-4
З-4	Сантехнические приборы и инсталляции: С-01, С-03, С-04, С-05, С-06		для Р-4
З-5	Керамогранит и плитка: 4 поз. по артикулу и формату, 51,59 м² по раскладке		для Р-9
З-6	Покрытие пола (доска) и плинтус: пом. 1, 5, 6, 7		для Р-12
З-7	Встроенная мебель по замеру цеха: М-04	6	для Р-15

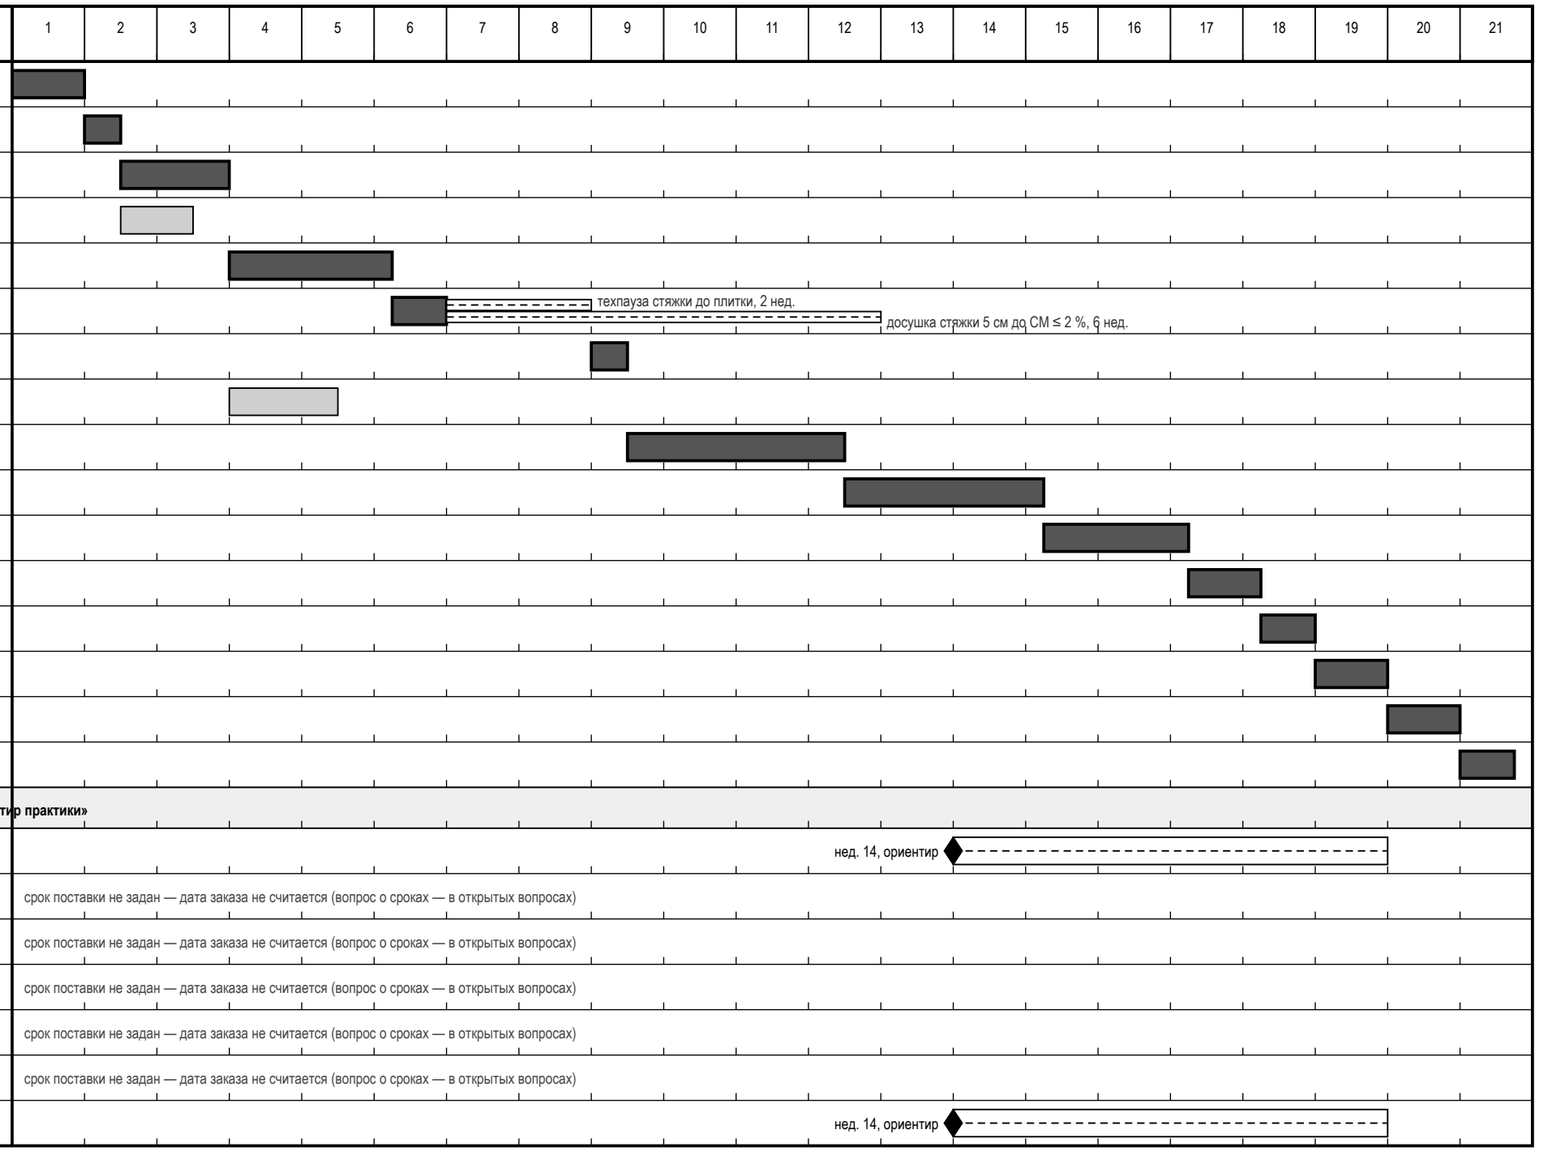

Итого: ≈ 20,75 нед. · жирная линия и тёмная полоса — критический путь

Примечания

1. Длительности этапов — типовые сроки по площади 68,47 м² (таблица «Свод для графика»: недели по этапам для 45, 80 и 120 м², середина вилки, линейная интерполяция); это ориентир, а не норма и не обещание бригады. Контрольный обмер — ориентир 0,5 нед. (в таблице нет).
2. Зависимости «после» — из графика закупок и работ (лист «График закупок и работ»); каждая работа начинается после конца предшественников. Техпаузы стоят отдельными полосами, а не спрятаны в длительности: стяжка → плитка — не менее 2 нед.; стяжка → чистовой пол — досушка стяжки 5 см до СМ ≤ 2 % — 6 нед. (ориентир «1 нед. на 1 см до 4 см, 5 см — 6 нед., 6 см — 8 нед.»; решает замер).
3. График последовательный и поэтому консервативный: в жизни шпаклёвка, плитка и досушка стяжки идут частично параллельно (таблица типовых сроков для 68,47 м²: 15–18 нед.). Совмещения — решение прораба после обмера.
4. Закупки: «заказать не позднее» = начало работы, которой нужна позиция, минус срок поставки. Срок поставки — из данных проекта (срок поставки позиции, срок изготовления обоев в отделке); если его нет, в графике стоит типовой диапазон практики с пометкой «ориентир» — это не срок поставщика, его надо получить до заказа. Кухню и встроенную мебель заказывают после замера по готовым стенам (после штукатурки). Позиции без срока дат заказа не имеют.

	Лист	№ док.	Подпись	Дата	Проект: Квартира 68 м², элитный модерн			
Дизайнер	Кырлан А.С.			13.11.26	Календарный график работ и закупок	Стадия	Лист	Листов
Проверил						П	С14	94
Н. контр.								
Утв.								

выпуск 13.11.2026 № c38d47cb31 · стр. 90 из 94

Приёмка по этапам: контрольные точки, допуски и акты скрытых работ

Этап	Контрольная точка (дальше не пускают без подписи)	Что проверяют	Чем	Допуск	Основание	Подпись	Акт скрытых работ / документ
Р-1	Демонтаж До начала демонтажа: запрошены документы на дом и БТИ	Что снимается и что не трогается: покрытия, отделка, дверные блоки; несущие стены и перегородки — без изменений	осмотр по плану демонтажа	снятое — только по плану; несущее не затрагивать	практика		Фото помещений до и после демонтажа; перечень снятого в журнале работ.
Р-2	Контрольный обмер Контрольный обмер на голых стенах сделан до заказа всего, что делают по размеру	Размеры помещений и проёмов, диагонали, положение стояков, щитка, каналов, толщины стен	рулетка, лазерный дальномер, уровень	допуск задаёт проект; расхождение с планом — в перечень открытых вопросов до заказа	практика		Протокол контрольного обмера с эскизом; расхождения занесены в открытые вопросы.
Р-3	Черновая электрика Черновая электрика: трассы, высоты подрозетников, замер изоляции подписаны до заделки	Сопротивление изоляции проводки (цепи до 1000 В)	мегаомметр	не менее 0,5 МОм	норматив (ПУЭ, гл. 1.8)		Акт скрытых работ на трассы проводки и слаботочные линии до закрытия штукатуркой и ГКЛ; исполнительная схема трасс с привязками; заземление и уравнивание потенциалов в санузле протокол и фото.
		Целостность и маркировка: PE жёлто-зелёный, N — синий, L — прочие цвета	визуально, прозвонка	каждый проводник промаркирован	практика		
		Высоты подрозетников и привязки — по плану розеток и выключателей	рулетка, уровень	по проекту; от чистого пола	практика		
Р-4	Черновая сантехника Черновая сантехника: опрессовка, отметки выводов, инсталляции подписаны до зашивки	Опрессовка водоснабжения: рабочее давление до 0,6 МПа — испытание 0,9 МПа; выше 0,6 МПа — по расчёту	опрессовочный насос, манометр	выдержка 10 мин (поквартирная); падение: пластик не более 0,06 МПа за 30 мин, сталь не более 0,05 МПа за 10 мин	практика (СП 73.13330)		Акт опрессовки (давление, время, результат); акт скрытых работ на трассы в стенах, полу и коробах; инсталляции, скрытые смесители, трапы — фото с рулеткой и отметками.
		Уклон канализации Ø40–50	уровень, построитель плоскостей	не менее 20 мм на 1 м	норматив (СП 30.13330)		
		Протечки в соединениях, сифоны, смесители, гибкая подводка	осмотр под давлением, салфетка на стыках	нет капель и влажных следов в контрольное время	практика		
		Отметки выводов и положение инсталляций до зашивки и гидроизоляции	рулетка в кадре, фото	по листу выводов	практика		
Р-5	Штукатурка Маяки стен проверены до штукатурки; коробки скрытых дверей стоят до штукатурки	Отклонение от вертикали (простая / улучшенная / высококачественная штукатурка)	отвес, лазерный уровень	3 / 2 / 1 мм на 1 м; не более 15 / 10 / 5 мм на высоту	практика (СП 71.13330.2017)		Фото коробок скрытых дверей с отметкой чистого пола — до штукатурки; класс штукатурки (простая / улучшенная / высококачественная) назван в договоре.
		Отклонение от горизонтали	уровень, правило	3 / 2 / 1 мм на 1 м; не более 15 / 10 / 5 мм на длину	практика (СП 71.13330.2017)		
		Неровности (плоскостность)	правило 2 м и щуп	до 5 / 3 / 2 мм на 1 м; не более 3 / 2 / 2 неровностей на 4 м²	практика (СП 71.13330.2017)		
		Влажность основания перед шпаклёвкой и отделкой	влагомер	верхние 20–30 мм — не более 5 % по массе	норматив (СП 71, табл. 7.2)		
Р-6	Стяжка Стяжка: подготовка, после заливки ровность, затем замер СМ перед чистовым полом	Ровность: просвет под рейкой 2 м	рейка 2 м, клиновой щуп	под паркет, ламинат — 2 мм; под гидроизоляцию до 4 мм; прочие покрытия — до 6 мм (цифры расходятся между источниками — сверить перед актом)	практика (СП 29.13330)		Акт скрытых работ на стяжку (толщина, армирование) до чистового пола; протокол ровности и протокол СМ-влажности; звукоизоляция и демпферная лента под стяжкой — фото и паспорт; контуры тёплого пола до заливки — схема укладки и замер сопротивления.
		Отклонение от горизонтали по помещению	уровень, нивелир	не более 0,2 % длины помещения	практика (СП 29.13330)		

	Лист	№ док.	Подпись	Дата	Проект: Квартира 68 м², элитный модерн			
Дизайнер	Кырлан А.С.			13.11.26	Чек-лист приёмки по этапам. Лист 1 из 3	Стадия	Лист	Листов
Проверил						П	С15	94
Н. контр.								
Утв.								

Приёмка по этапам: контрольные точки, допуски и акты скрытых работ (продолжение)

Этап	Контрольная точка (дальше не пускают без подписи)	Что проверяют	Чем	Допуск	Основание	Подпись	Акт скрытых работ / документ
		Число точек измерения	рейка	не менее 3 на 30 м² или 1 на небольшое помещение	практика		
		Отслоения и пустоты	простукивание молотком или киянкой	глухой звук — зона вскрывается и переделывается	практика		
		Влажность перед укладкой доски: цементная стяжка	влагомер; СМ-замер	ЦПС не более 2,0 % СМ (с тёплым полом не более 1,8 %); влагомер для плитки — не более 5 %	практика (СП 71; рекомендации производителей)		
Р-7	Гидроизоляция Гидроизоляция: пролив 24 ч подпись до плитки	Заведение на стены не ниже 200 мм от чистого пола; за ванной — 300 мм выше борта; в душе без поддона — на высоту лейки	рулетка	не менее 200 мм	норматив (СП 71.13330.2017, п. 8.6.5); остальное — практика		Акт теста проливом, фото узлов и высоты заведения на стены — до плитки.
		Тест проливом: слой воды 10–30 мм, контроль уровня и потолка соседа снизу	линейка, визуально	24 ч (минимум 12 ч); падения уровня и протечки нет	практика		
		Два слоя обмазки с межслойной сушкой, лента в углах и манжеты на выводах	визуально	по инструкции производителя	практика		
Р-8	ГКЛ Короба, ниши и потолки: черновые сети в зоне коробов приняты до обшивки	Шаг саморезов, отступ от кромки, заделка стыков (как у перегородок)	рулетка, визуально	потолок 150 мм; кромка 5–10 мм; стык — лента и 2 слоя шпаклёвки	практика (СП 163.1325800.2014)		Акт скрытых работ: каркас ГКЛ, закладные, звукоизоляция — фото до обшивки; воздуховоды в коробах и за потолком — фото и схема.
		Закладные под тяжёлое, карнизы, подвесные светильники на месте до обшивки	фото с привязками	по плану потолков и узлам	практика		
		Ревизионные люки: доступ к арматуре и ревизиям сохранён	осмотр	по листу ВК	практика		
Р-9	Плитка Раскладка плитки: первая плита и первый ряд проверены по развёртке; плитка выбрана, калибр партии измерен	Уступы между смежными плитками	линейка, на просвет	не более 1 мм	норматив (СП 71.13330.2017)		Раскладка подписана до начала плитки; протокол первого ряда; акт теста проливом приложен (этап гидроизоляции).
		Ширина шва и его прямолинейность	линейка, калибр	до 6 мм ручная укладка; фактическая по проекту ±0,5 мм	практика		
		Отклонение рядов от вертикали и горизонтали	уровень, правило, отвес	1,5 мм на 1 м длины	практика		
		Ровность облицовки	правило 2 м и щуп	не более 2–4 мм (цифра расходится по источникам)	практика		
		Пустоты под плиткой	простукивание всей площади	до 10 % площади допустимо; свыше 25 % под одной плиткой — брак	практика		
Р-10	Шпаклёвка Шпаклёвка Q3/Q4: проверка боковым светом до окраски	Класс основания под окраску: Q3 — сплошное финишное шпаклевание; Q4 — под направленный свет	переносной прожектор у поверхности под острым углом	Q3: царапины от абразива до 0,5 мм; Q4 — без видимых царапин и теней; неровность на 2 м: Q3 — 1 мм, Q4 — 0,5 мм	практика (Q-классы — не норматив СП, а согласованный критерий)		Класс (Q3 или Q4) назван в договоре; грунтование и армирование стыков перед шпаклёвкой — запись в журнале.
Р-11	Окраска Выкрасы утверждены, колеровка одной партией	Окраска без полос, подтёков, пропусков; цвет — по колерной карте	боковой свет, образец выкраса	без видимых дефектов при боковом свете	практика		Утверждённые выкрасы; остаток колеровки одной партии — для подкраски.
		Основание сухое, огрунтованное; защита от прямого солнца при высыхании	осмотр	по ТУ краски	норматив (СП 71.13330.2017, п. 7.5.2)		

	Лист	№ док.	Подпись	Дата	Проект: Квартира 68 м², элитный модерн			
Дизайнер	Кырлан А.С.			13.11.26	Чек-лист приёмки по этапам. Лист 2 из 3	Стадия	Лист	Листов
Проверил						П	С16	94
Н. контр.								
Утв.								

выпуск 13.11.2026 № c38d47cb31 · стр. 92 из 94

Приёмка по этапам: контрольные точки, допуски и акты скрытых работ (продолжение)

Этап	Контрольная точка (дальше не пускают без подписи)	Что проверяют	Чем	Допуск	Основание	Подпись	Акт скрытых работ / документ
Р-12	Чистовые полы Чистовые полы: влажность, ровность, уступы, зазоры — до укладки доски; мокрые работы закончены	Деформационный зазор у стен и порогов (доска, ламинат)	линейка, клинья при укладке	8–15 мм (чаще 10 мм); у ламината 5–10 мм по СП 71	практика (требования производителей); норматив (СП 71, п. 8.10.14)		Протокол СМ-влажности стяжки до укладки; паспорт и партия доски.
		Перепад основания под покрытие	правило 2 м и щуп	не более 2 мм на 2 м	практика		
		Зазоры и перепады между досками; скрип; видимый зазор в замке — брак	щуп, рука, шаг	«ступеньки» нет	практика		
		Влажность помещения при укладке и после	гигрометр	не более 60 %, без сквозняков	норматив (СП 71, п. 8.1.7)		
Р-13	Двери и плинтусы Полотна и плинтусы — после чистового пола; скрытые полотна после чистовой отделки стен	Отклонение коробки от вертикали	отвес, уровень	1,5 мм на 1 м, не более 3 мм на коробку	практика (ТР 105-00, пересказ)		Коробки скрытых дверей приняты до штукатурки (этап штукатурки); паспорт на полотна.
		Зазор между полотном и коробкой по периметру	щуп	2–4 мм по бокам и верху (единого норматива нет)	практика		
		Открывание и закрывание: без перекоса, плавный ход петель и доводчика	визуально, от руки	без задевания коробки и пола	практика		
Р-14	Чистовая электрика и сантехника Чистовая электрика и сантехника: протокол электролаборатории и проверка УЗО до подписи акта	УЗО: кнопка «Тест»; время отключения; ток отключения	кнопка на аппарате; прибор проверки УЗО (не мультиметр)	отключает; не более 0,3 с; 50–100 % от IΔn	практика измерений		Протокол измерений аккредитованной электролаборатории (изоляция по группам, УЗО, PE, фаза-ноль); исполнительная схема щита; акт опрессовки приложен (этап ВК).
		Сопротивление изоляции готовых линий; петля фаза-ноль для срабатывания автоматов	мегаомметр; прибор петли фаза-ноль	изоляция не менее 0,5 МОм; петля — по проекту	норматив (ПУЭ, гл. 1.8) / по проекту		
		Смесители, сифоны, гибкая подводка: пробный пуск воды	визуально под нагрузкой	нет подтёков в контрольное время	практика		
Р-15	Кухня и мебель Кухня и мебель: замер кухни снят по готовым стенам; чистовая электрика и сантехника подведены	Привязка выводов и розеток к модулям кухни; вытяжка, вентиляция	рулетка, сверка с листом кухни	по проекту кухни	практика		Акт передачи кухни; паспорта техники и гарантийные талоны.
		Тяга вентиляции у решёток	лист бумаги у решётки	бумага притягивается; при сомнениях — замер анемометром	практика		
Р-16	Сдача Финальная приёмка по таблицам СП 71: дефектная ведомость и акт	Стены, потолки, полы, плитка, двери, окна осмотр по чек-листу этапов выше	правило 2 м, уровень, щуп, боковой свет, влагомер	по таблицам выше	практика		Дефектная ведомость и акт приёмки; гарантия: по умолчанию претензии по качеству работ — 2 года, в договоре прописывается отдельно.
		Полный пакет документов: акты скрытых работ, протокол электролаборатории, акт опрессовки, исполнительные схемы, гарантийные обязательства	комплектность	пакет собран до подписи акта	практика		

Примечания

1. Метка основания: «норматив» — цифра подтверждена текстом СП, ГОСТ или ПУЭ; «практика» — отраслевая конвенция или один источник: к спору не годится без сверки первоисточника (СП 71.13330.2017, СП 29.13330, СП 163.1325800.2014, ПУЭ гл. 1.8, СП 73.13330, СП 30.13330).
2. Класс штукатурки (простая / улучшенная / высококачественная) и класс основания под окраску (Q3 или Q4) называются в договоре подряда: допуск выбирается по ним. Q-классы — не норматив, а согласованный сторонами критерий.
3. Акт скрытых работ подписывают до того, как работа закрыта следующим слоем (штукатуркой, плиткой, стяжкой, обшивкой): постфактум он слабее — осматривать нечего. Подписывают заказчик (или технадзор), подрядчик; при перепланировке — автор проекта. Каждую зону снимают до закрытия с рулеткой в кадре и привязкой к стене.
4. По умолчанию, если срок не прописан в договоре, претензии по качеству работ можно предъявить в течение 2 лет со дня приёмки; в договоре гарантийный срок и сроки на скрытые работы рекомендуется назвать явно.

	Лист	№ док.	Подпись	Дата	Проект: Квартира 68 м², элитный модерн			
Дизайнер	Кырлан А.С.			13.11.26	Чек-лист приёмки по этапам. Лист 3 из 3	Стадия	Лист	Листов
Проверил						П	С17	94
Н. контр.								
Утв.								

выпуск 13.11.2026 № c38d47cb31 · стр. 93 из 94

Какому мастеру какие листы (номера — как в штампе)

Мастер	Что делает по альбому	Листы	Кроме чертежей — документы	Листов
Замерщик и прораб (до начала работ)	Контрольный обмер на голых стенах, сверка размеров и диагоналей, ответы на открытые вопросы до заказа	12, 14, 72–74	Задание на контрольный обмер; лист открытых вопросов	5
Гипсокартонщик и монтажник перегородок	Демонтаж и возведение перегородок, каркас, короба инсталляции, ниши, потолки; закладные под навесное	15–17, 38–40	Ведомость материалов каркаса; акт скрытых работ на каркас	6
Электрик	Группы щита, подрозетники и высоты, трассы, свет, управление светом, слаботочка, тёплый пол	41–49, 55–71	Таблица нагрузок; ведомость изделий; протокол электролаборатории	26
Сантехник	Выводы воды и канализации, разводка, аксонометрии, инсталляции, короба стояков	26–34, 55–71	Спецификация ВК; акт опрессовки; акт пролива	26
Монтажник вентиляции, отопления и кондиционеров	Вентиляция, радиаторы и тёплые полы, кондиционеры: места, размеры, трассы и дренаж	50–51	Акт опрессовки азотом (кондиционеры); фото воздуховодов до закрытия	2
Штукатур, шпаклёвщик, маляр, паркетчик	Основание стен, окраска и обои по колерной карте, полы и пороги, плинтус, узлы стыков	18–19, 52, 55–71, С1–С3, С13	Колерная карта и выкрасы; спецификация отделочных материалов	24
Плиточник	Раскладка и подрезка плитки стен, пола и фартука, гидроизоляция, швы, выводы в плитке	31–33, 35–36, 53–71, С13	Ведомость плитки; акт теста проливом	25
Монтажник дверей и окон	Заполнение проёмов: размеры коробок, открывание, пороги, скрытые двери	37	Ведомость проёмов; паспорта на полотна	1
Мебельщик, кухонный монтажник	Кухня и мебель на заказ: габариты, членение, фурнитура, связка с электрикой и сантехникой	16–17, 20–25, Д1–Д2	Ведомость изделий; замер кухни по готовым стенам	10
Заказчик и комплектатор	Что и когда покупать, сколько с запасом, во что это обойдётся; свет, декор и текстиль; визуализации как должно получиться	1–11, 13, 48, С4–С12, С14	Список покупок; смета; календарный график	23
Прораб и технадзор (приёмка)	Приёмка этапов, акты скрытых работ, дефектная ведомость	С14–С18	Чек-лист приёмки по этапам; календарный график	5

Примечания

1. Номера листов — как в основной надписи: основные подряд (1, 2, 3…), «Д» — детализация мебели, «С» — ведомости, спецификации, узлы и сметы, «П» — приложение единого комплекта. «12–18» — все листы с 12 по 18.
2. Лист может быть у нескольких мастеров: развёртка стены нужна электрику (высоты точек), сантехнику (выводы), отделочнику (материалы) и плиточнику (раскладка). Общие листы (обмер, список листов, перечень вопросов) прораб раздаёт всем.
3. Мастер работает по чертежам и берёт в руки то, что назначено ему здесь; закупки, смету и график ведёт заказчик с прорабом. Лист, которого нет в таблице ни у одного мастера, — вопрос прорабу: чей он.

	Лист	№ док.	Подпись	Дата	Проект: Квартира 68 м², элитный модерн			
Дизайнер	Кырлан А.С.			13.11.26	Лист → мастер	Стадия	Лист	Листов
Проверил						П	С18	94
Н. контр.								
Утв.								

выпуск 13.11.2026 № c38d47cb31 · стр. 94 из 94