
L

LINEA

ДИЗАЙН-ПРОЕКТ ИНТЕРЬЕРА

Трёхкомнатная квартира

Warm Contemporary

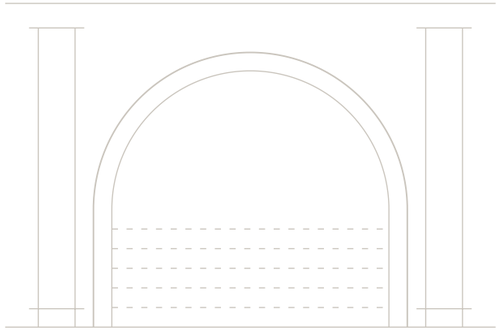

ПАЛИТРА ОТДЕЛКИ

F&B No. 241	V503	F&B No. 30	H487	NCS S 3005-Y20
47 %	37 %	15 %	текстиль, декор	текстиль, декор

АВТОР ПРОЕКТА

Кырлан Александр Сергеевич

Ноябрь 2026



Визуализация гостиной · 3D

ОБЩАЯ ПЛОЩАДЬ	ПОМЕЩЕНИЙ	СТАДИЯ	ШИФР	ОСНОВА
78,95 м²	8, из них жилых 3	Рабочий проект · предварительно	ГД-2026-003-АИ	план заказчика, без обмера

Изм.	Кол.уч	Лист	№ док.	Подп.	Дата
Разраб.		Кырлан А.С.			13.11.26
Пров.					
ГИП					
Н. контр.					
Утв.					

ГД-2026-003-АИ

Трёхкомнатная квартира

Общая площадь 78,95* м² · * размеры со скана, не замерены (реестр — л. 6–11, К-13)

Дизайн-проект интерьера трёхкомнатной квартиры

Стадия	Лист	Листов
РП	1	132

Титульный лист

М б/м

Кырлан Александр Сергеевич

выпуск 13.11.2026 № 6f3a8abb2c · стр. 1 из 157

Общие данные

Комплект ГД-2026-003-АИ · Квартира 3К · Warm Contemporary

ПРЕДВАРИТЕЛЬНО · не для производства работ · открыто пунктов: 28 (реестр — л. 6–11)

Допущения и предложения на листе. См. лист открытых вопросов (листы 6–11).

Ведомость рабочих чертежей основного комплекта ГД-2026-003-АИ

Лист	Наименование	Примечание
1	Титульный лист	
2	Общие данные	
3	Общие данные	
4	Общие данные	
5	Общие данные	
6	Открытые вопросы, принятые допущения и конфликты. Лист 1 из 6	
7	Открытые вопросы, принятые допущения и конфликты. Лист 2 из 6	
8	Открытые вопросы, принятые допущения и конфликты. Лист 3 из 6	
9	Открытые вопросы, принятые допущения и конфликты. Лист 4 из 6	
10	Открытые вопросы, принятые допущения и конфликты. Лист 5 из 6	
11	Открытые вопросы, принятые допущения и конфликты. Лист 6 из 6	
12	Задание на контрольный обмер и обследование. Лист 1 из 5	
13	Задание на контрольный обмер и обследование. Лист 2 из 5	
14	Задание на контрольный обмер и обследование. Лист 3 из 5	
15	Задание на контрольный обмер и обследование. Лист 4 из 5	
16	Задание на контрольный обмер и обследование. Лист 5 из 5	
17	График закупок и работ. Лист 1 из 4	
18	График закупок и работ. Лист 2 из 4	
19	График закупок и работ. Лист 3 из 4	
20	График закупок и работ. Лист 4 из 4	
21	Календарный график работ и закупок	
22	Чек-лист приёмки по этапам. Лист 1 из 4	
23	Чек-лист приёмки по этапам. Лист 2 из 4	
24	Чек-лист приёмки по этапам. Лист 3 из 4	
25	Чек-лист приёмки по этапам. Лист 4 из 4	
26	Лист → мастер	
27	Обмерный план	
28	План демонтажа и монтажа перегородок	
29	Ведомость демонтажа и монтажа перегородок	
30	План дверей и ведомость заполнения проёмов	

Ведомость рабочих чертежей основного комплекта ГД-2026-003-АИ (продолжение)

Лист	Наименование	Примечание
31	Концепция интерьера	
32	План расстановки мебели	
33	Спецификация мебели и оборудования	
34	Спецификация мебели и оборудования (продолжение)	
35	Спецификация мебели и оборудования (продолжение)	
36	Спецификация мебели и оборудования (продолжение)	
37	План розеток и электровыводов	
38	План освещения	
39	План выключателей и схема включения	
40	Ведомость электроточек и изделий	
41	Ведомость электроточек и изделий (продолжение)	
42	Однолинейная схема щита	
43	План принципиальных трасс	
44	Таблица нагрузок щита	
45	План слаботочных сетей	
46	План вентиляции	
47	План отопления	
48	План выводов сантехники	
49	Схема разводки водопровода и канализации	
50	Аксонометрическая схема В1 (холодное водоснабжение)	
51	Аксонометрическая схема Т3 (горячее водоснабжение)	
52	Аксонометрическая схема К1 (канализация)	
53	Развёртки мокрых зон: выводы ВК. Ванная	

Общие указания — лист 5: ±0,000 — чистый пол; несущие конструкции и сети дома — по отдельному проекту; скрытые работы — по актам. Открытые вопросы и допущения — листы 6–11.

Изм.	Кол.уч	Лист	№ док.	Подп.	Дата
Разраб.		Кырлан А.С.			13.11.26
Пров.					
ГИП					
Н. контр.					
Утв.					

ГД-2026-003-АИ

Трёхкомнатная квартира

Общая площадь 78,95* м² · * размеры со скана, не замерены (реестр — л. 6–11, К-13)

Дизайн-проект интерьера трёхкомнатной квартиры

Стадия	Лист	Листов
РП	2	132

Общие данные

М б/м

Кырлан Александр Сергеевич

выпуск 13.11.2026 № 6f3a8abb2c · стр. 2 из 157

Общие данные

Комплект ГД-2026-003-АИ · лист 2 общих данных (продолжение)

Допущения и предложения на листе. См. лист открытых вопросов (листы 6–11).

Ведомость рабочих чертежей основного комплекта ГД-2026-003-АИ (продолжение)

Лист	Наименование	Примечание
54	Развёртки мокрых зон: выводы ВК. Кухня-гостиная	
55	Развёртки мокрых зон: выводы ВК. Санузел 2	
56	Спецификация сантехнического оборудования	
57	Техническое задание на подбор светильников	
58	Схема каркаса перегородки П-1	
59	План потолков	
60	Разрезы и узлы потолков	
61	Сечения потолков М 1:10	
62	Раскладка плитки. Планы полов	
63	Раскладка плитки. Прихожая. Фартук кухни	
64	Раскладка плитки. Ванная. Развёртки стен	
65	Раскладка плитки. Санузел 2. Развёртки стен	
66	План полов	
67	Ведомость отделки помещений. Лист 1 из 2	
68	Ведомость отделки помещений. Лист 2 из 2	
69	Колерная карта	
70	Спецификация отделочных материалов	
71	Концепция декора и визуализации	
72	План текстиля и декора	
73	Шторы и карнизы	
74	Ведомость текстиля	
75	Ведомость декора	
76	Схемы развески	
77	Встроенная мебель. Схема расположения	
78	Шкаф распашной С5	
79	Система хранения Г1	
80	Шкаф-купе М16	
81	Кухня (пом. 6). Развёртка гарнитура	
82	Кухня (пом. 6). Развёртка гарнитура: вид без фасадов и разрезы	
83	Кухня (пом. 6). Монтажная схема	

Ведомость рабочих чертежей основного комплекта ГД-2026-003-АИ (продолжение)

Лист	Наименование	Примечание
84	Кухня (пом. 6). Столешница: план	
85	Шкафы. Монтажная схема	
86	Ведомости изделий, техники и фурнитуры	
87	Сводка листовых материалов и кромки	
88	Реестр марок отделки и позиций альбома	
89	Схема расположения развёрток и узлов	
90	Развёртка стены А. Спальня 1 (пом. 1)	
91	Развёртка стены Б. Спальня 1 (пом. 1)	
92	Развёртка стены В. Спальня 1 (пом. 1)	
93	Развёртка стены Г. Спальня 1 (пом. 1)	
94	Развёртки стен А, Б. Ванная (пом. 2)	
95	Развёртки стен В, Г. Ванная (пом. 2)	
96	Развёртки стен А, Б. Гардеробная (пом. 3)	
97	Развёртки стен В, Г. Гардеробная (пом. 3)	
98	Развёртка стены А. Спальня 2 (пом. 4)	
99	Развёртка стены Б. Спальня 2 (пом. 4)	
100	Развёртка стены В. Спальня 2 (пом. 4)	
101	Развёртка стены Г. Спальня 2 (пом. 4)	
102	Развёртка стены А. Прихожая (пом. 5)	
103	Развёртки стен Б, В. Прихожая (пом. 5)	
104	Развёртка стены Г. Прихожая (пом. 5)	
105	Развёртка стены Б2. Кухня-гостиная (пом. 6), кухонный фронт	
106	Развёртка стены В1. Кухня-гостиная (пом. 6), кухонный фронт	

Общие указания — лист 5: ±0,000 — чистый пол; несущие конструкции и сети дома — по отдельному проекту; скрытые работы — по актам. Открытые вопросы и допущения — листы 6–11.

Изм.	Кол.уч	Лист	№ док.	Подп.	Дата	ГД-2026-003-АИ			
						Трёхкомнатная квартира Общая площадь 78,95* м² · * размеры со скана, не замерены (реестр — л. 6–11, К-13)			
Разраб.		Кырлан А.С.			13.11.26	Дизайн-проект интерьера трёхкомнатной квартиры	Стадия	Лист	Листов
Пров.							РП	3	132
ГИП						Общие данные М б/м	Кырлан Александр Сергеевич		
Н. контр.									
Утв.									

выпуск 13.11.2026 № 6f3a8abb2c · стр. 3 из 157

Общие данные

Комплект ГД-2026-003-АИ · лист 3 общих данных (продолжение)

Ведомость рабочих чертежей основного комплекта ГД-2026-003-АИ (продолжение)

Лист	Наименование	Примечание
107	Развёртка стены А. Кухня-гостиная (пом. 6)	
108	Развёртки стен Б1, В2. Кухня-гостиная (пом. 6)	
109	Развёртки стен Г1, Г2. Кухня-гостиная (пом. 6)	
110	Развёртки стен А, Б. Санузел 2 (пом. 7)	
111	Развёртки стен В, Г. Санузел 2 (пом. 7)	
112	Развёртки стен А, Б. Коридор (пом. 8)	
113	Развёртки стен В, Г. Коридор (пом. 8)	
114	Узлы. Лист 1 из 2	
115	Узлы. Лист 2 из 2	
116	Ведомость объёмов работ	
117	Ведомость объёмов работ (продолжение)	
118	Ведомость объёмов работ (продолжение)	
119	Ведомость объёмов работ (окончание)	
120	Спецификация материалов	
121	Спецификация материалов (продолжение)	
122	Спецификация материалов (окончание)	
123	Смета ориентировочная	
124	Смета ориентировочная (окончание)	
125	Смета проекта: этапы, помещения, итог	
126	Смета проекта: этапы, помещения, итог (продолжение)	
127	Смета проекта: этапы, помещения, итог (окончание)	
128	Смета материалов с ценами	
129	Смета материалов с ценами (продолжение)	
130	Смета материалов с ценами (продолжение)	
131	Смета материалов с ценами (продолжение)	
132	Смета материалов с ценами (окончание)	

Ведомость ссылочных и прилагаемых документов

Обозначение	Наименование	Примечание
	Ссылочные документы	
ГОСТ 21.201-2011	СПДС. Условные графические изображения элементов зданий, сооружений и конструкций	
ГОСТ 21.205-2016	СПДС. Условные обозначения элементов санитарно-технических систем	
ГОСТ 21.210-2014	СПДС. Изображения условные графические электрооборудования и проводок на планах	
ГОСТ 2.306-68	ЕСКД. Обозначения графические материалов и правила их нанесения на чертежах	
	Прилагаемые документы	
ГД-2026-003-АИ.В1	Визуализация. Вид сверху (3D): планировка с мебелью, текстилем и декором	альбом визуализаций
ГД-2026-003-АИ.В2	Визуализация. Потолок: Санузел 2 (пом. 7)	
ГД-2026-003-АИ.В3	Визуализация. Потолок: Спальня 1 (пом. 1)	
ГД-2026-003-АИ.В4	Визуализация. Потолок: Спальня 2 (пом. 4)	
ГД-2026-003-АИ.В5	Визуализация. Потолок: Коридор (пом. 8)	
ГД-2026-003-АИ.В6	Визуализация. Потолок: Прихожая (пом. 5)	
ГД-2026-003-АИ.В7	Визуализация. Потолок: Кухня-гостиная (пом. 6)	
ГД-2026-003-АИ.В8	Визуализация. Интерьер: Ванная (пом. 2), стена Б	
ГД-2026-003-АИ.В9	Визуализация. Интерьер: Ванная (пом. 2), стена Г	
ГД-2026-003-АИ.В10	Визуализация. Интерьер: Санузел 2 (пом. 7), стена Б	
ГД-2026-003-АИ.В11	Визуализация. Интерьер: Спальня 1 (пом. 1), стена А	
ГД-2026-003-АИ.В12	Визуализация. Интерьер: Спальня 1 (пом. 1), стена Б	
ГД-2026-003-АИ.В13	Визуализация. Интерьер: Спальня 2 (пом. 4), стена А	
ГД-2026-003-АИ.В14	Визуализация. Интерьер: Спальня 2 (пом. 4), стена В	
ГД-2026-003-АИ.В15	Визуализация. Интерьер: Спальня 2 (пом. 4), стена Г	
ГД-2026-003-АИ.В16	Визуализация. Интерьер: Коридор (пом. 8), стена А	

Допущения и предложения на листе

Основа листа: размеры сняты со скана плана заказчика по размерным цепочкам, контрольный обмер на объекте не выполнялся (К-13); высота потолка 2700 мм принята: на плане заказчика не указана (К-11); толщины стен приняты: наружные 250 мм, перегородки 150 мм (на плане 85–190 мм) (К-13); разрешённая мощность 15 кВт принята по типовой квартире, технических условий нет (К-14); утолщение стены 190 × 1360 мм и элемент 1470 × 160 мм плана заказчика не определены (К-12); ниши санузла 2 закрыты перегородкой и фальш-стеной: проектное решение, на плане заказчика ниша у входа открыта (К-18); несущие стены не определены: до технического заключения все существующие стены считаются несущими (К-20); окна существующие и сохраняются; подоконная доска и глубина откосов не заданы — приняты, не замерены (К-27); подрайон климата не задан — принят не северный (жилые от 2,5 м) (К-29).

См. лист открытых вопросов (лист 7, записи К-11–К-14, К-18, К-20; лист 8, записи К-27, К-29).

Общие указания — лист 5: ±0,000 — чистый пол; несущие конструкции и сети дома — по отдельному проекту; скрытые работы — по актам. Открытые вопросы и допущения — листы 6–11.

Изм.	Кол.уч	Лист	№ док.	Подп.	Дата
Разраб.		Кырлан А.С.			13.11.26
Пров.					
ГИП					
Н. контр.					
Утв.					

ГД-2026-003-АИ

Трёхкомнатная квартира

Общая площадь 78,95* м² · * размеры со скана, не замерены (реестр — л. 6–11, К-13)

Дизайн-проект интерьера трёхкомнатной квартиры

Стадия	Лист	Листов
РП	4	132

Общие данные

М б/м

Кырлан Александр Сергеевич

выпуск 13.11.2026 № 6f3a8abb2c · стр. 4 из 157

Общие данные

Комплект ГД-2026-003-АИ · лист 4 общих данных (продолжение)

Ведомость ссылочных и прилагаемых документов (продолжение)

Обозначение	Наименование	Примечание
ГД-2026-003-АИ.В17	Визуализация. Интерьер: Прихожая (пом. 5), общий вид	
ГД-2026-003-АИ.В18	Визуализация. Интерьер: Кухня-гостиная (пом. 6), стена Б	
ГД-2026-003-АИ.В19	Визуализация. Интерьер: Кухня-гостиная (пом. 6), стена В	
ГД-2026-003-АИ.В20	Визуализация. Интерьер: Кухня-гостиная (пом. 6), стена Г	
ГД-2026-003-АИ.В21	Визуализация. Интерьер: Гардеробная (пом. 3), общий вид	

Состав дизайн-проекта

Раздел	Состав	Листы
Обложка	Дизайн-проект интерьера трёхкомнатной квартиры; Трёхкомнатная квартира; автор проекта — Кырлан Александр Сергеевич	1 с.
Концепция	Стиль Современный (контемпорари): концепция интерьера, палитра и материалы (колерная карта — лист 69)	л. 31
Визуализации	21 изобр.: Вид сверху (3D): планировка с мебелью, текстилем и декором; Потолок: Санузел 2; Потолок: Спальня 1; Потолок: Спальня 2; Потолок: Коридор; Потолок: Прихожая; Потолок: Кухня-гостиная; Ванная, стена Б; Ванная, стена Г; Санузел 2, стена Б; Спальня 1, стена А; Спальня 1, стена Б; Спальня 2, стена А; Спальня 2, стена В; Спальня 2, стена Г; Коридор, стена А; Прихожая, общий вид; Кухня-гостиная, стена Б; Кухня-гостиная, стена В; Кухня-гостиная, стена Г; Гардеробная, общий вид	В1–В21
Рабочие чертежи	планы, развёртки, узлы (развёртки и узлы — листы 53–55, 89, 94–97, 103, 108–115)	л. 1–132
Спецификации и ведомости	оборудование, изделия, отделка, электроточки	л. 29, 30, 33–36, 40, 41, 56, 67–70, 74, 75, 116–122

Условные обозначения

- контрольный отрезок 1000 мм натуры: по нему проверяют печать 1:1
- отметка уровня, м: ±0,000 — чистый пол жилых помещений
- А — марка развёртки: буква стены, стрелка — взгляд
- О1 — марка отделки по реестру отделки альбома
- выноска узла: над полкой — узел, под полкой — лист

Допущения и предложения на листе

Основа листа: размеры сняты со скана плана заказчика по размерным цепочкам, контрольный обмер на объекте не выполнялся (К-13); высота потолка 2700 мм принята: на плане заказчика не указана (К-11); толщины стен приняты: наружные 250 мм, перегородки 150 мм (на плане 85–190 мм) (К-13); разрешённая мощность 15 кВт принята по типовой квартире, технических условий нет (К-14); утолщение стены 190 × 1360 мм и элемент 1470 × 160 мм плана заказчика не определены (К-12); ниши санузла 2 закрыты перегородкой и фальш-стеной: проектное решение, на плане заказчика ниша у входа открыта (К-18); несущие стены не определены: до технического заключения все существующие стены считаются несущими (К-20); окна существующие и сохраняются; подоконная доска и глубина откосов не заданы — приняты, не замерены (К-27); подрайон климата не задан — принят не северный (жилые от 2,5 м) (К-29).
См. лист открытых вопросов (лист 7, записи К-11–К-14, К-18, К-20; лист 8, записи К-27, К-29).

Общие указания

1. Рабочие чертежи интерьера разработаны на основании задания на проектирование и обмерного плана (лист 27). Объект: Трёхкомнатная квартира; автор проекта — Кырлан Александр Сергеевич; общая площадь 78,95 м², жилая 59,75 м², помещений 8.
2. Рабочие чертежи выполнены в соответствии с заданием на проектирование и нормативными документами, перечисленными в п. 4.
3. Открытые вопросы, принятые допущения и конфликты между разделами, не снятые к выпуску комплекта, сведены в таблицы на листах 6–11. До ответа по пункту таблицы показанное на указанном там листе — допущение, а не утверждённое решение: комплект по этим листам предварительный.
4. Нормативные документы, на которые есть ссылки в листах комплекта: ГОСТ Р 21.101-2026; ГОСТ 21.501-2018; ГОСТ 2.302-68; ГОСТ 2.303-68; ГОСТ 2.304-81; ГОСТ 2.307-2011; СП 54.13330.2022; СП 71.13330.2017; СП 73.13330.2016; ПУЭ (7-е изд.), гл. 1.8, 7.1; ГОСТ Р 50571.7.701-2024; СанПиН 1.2.3685-21; ГОСТ 2.702; ГОСТ 2.755; ГОСТ 21.110-2013; ГОСТ 21.601; ГОСТ 13996-2019; ГОСТ 31173-2016; ГОСТ 31565-2012; ГОСТ 32414-2013; ГОСТ 32415-2013; ГОСТ 32614-2012; ГОСТ Р 56387-2018; СП 29.13330.2011; СП 30.13330.2020; СП 51.13330.2011; СП 131.13330; СП 163.1325800.2014; СП 256.1325800.2016. Документы из ведомости ссылочных документов здесь не повторяются.
5. За отметку ±0,000 принят уровень чистого пола жилых помещений квартиры (относительная отметка; абсолютная — по проекту дома). Отметка чистого пола мокрых помещений — −0,015. Размеры — в миллиметрах, отметки — в метрах, площади — в м²; высоты установки Н от чистого пола своего помещения до оси изделия.
6. Несущие конструкции, общедомовые стояки, вентиляционные каналы и инженерные сети дома настоящим комплектом не изменяются. Работы, затрагивающие их (проём или штраба в несущей стене, перенос стояка, врезка в вентканал, расширение мокрой зоны), выполняются только по отдельному проекту, к которому прилагается техническое заключение о допустимости и безопасности работ, выданное автором проекта дома или организацией с допуском на обследование, и который согласован в установленном порядке (Жилищный кодекс РФ, ст. 25–29).
7. Трассы инженерных сетей на листах — принципиальные. Расчёты электрических нагрузок и токов КЗ, гидравлики, воздухообмена, освещённости и нагрузок на перекрытие выполняются в проектах ЭОМ, ВК, ОВ и КР организацией с допуском СРО; фактические трассы до закрытия отделкой фиксируются исполнительными схемами.
8. Стиль интерьера — Современный (контемпорари). Палитра проекта: основной 60 % — Tikkurila V503 «Winter», Farrow & Ball No. 241 «Skimming Stone»; дополнительный 30 % — Tikkurila H487 «Pumice»; акцент 10 % — Farrow & Ball No. 30 «Hague Blue». Коды цвета — по веерам производителей; цвет утверждается по выкрасу на объекте при освещении проекта.
9. Площади поверхностей — по чистым граням стен до отделки: стены = периметр × высоту от чистого пола помещения до низа потолка минус проёмы (облицовка плиткой — до верха облицовки); плинтус = периметр минус дверные проёмы; пол и потолок — по площади помещения. Количество плиток — по раскладке. Способ один для всех листов комплекта (ведомость отделки, колерная карта, раскладка плитки, развёртки).
10. Марки: стены помещения на всех листах — А (верхняя по плану), Б (правая), В (нижняя), Г (левая); марка отделки О — одна на весь альбом; реестр марок отделки (с позициями колерной карты той же отделки) и марки позиций по видам — на листе 88.
11. Развёртки стен выполнены по всем помещениям для стен с электроточками, мебелью, декором и отделкой: санузлы и кухонный фронт — в М 1:25, остальные стены — в М 1:25; расположение развёрток и узлов — на листе 89, узлы — на листе 114.
12. Перечень скрытых работ, на которые составляются акты освидетельствования (форма по приказу Минстроя России № 344/пр): гидроизоляция пола и стен мокрых помещений (с тестом проливом); стяжка пола (толщина, прочность, влажность основания); скрытая электропроводка (за потолком и в штробах стен; условия штробления — в следующем пункте); трубопроводы водоснабжения и канализации до закрытия (опрессовка, уклоны); закладные и усиления под подвесные приборы, мебель и тяжёлый декор, рамы инсталляций; короба дверей скрытого монтажа до штукатурки; каркасы ГКЛ потолков, коробов и перегородок до обшивки.
13. Скрытая электропроводка: за потолком и в штробах стен. Штробы в стенах выполняются только после технического заключения о несущих конструкциях; до заключения несущие стены не определены, и все стены считаются несущими; объём штроб — в ведомости объёмов работ, строка «Штробы в стенах» (вертикальные спуски; объём не меньше фактического, горизонтальные трассы — по исполнительной схеме).
14. Критерии приёмки: допуски отделочных покрытий — по СП 71.13330.2017; испытания систем водоснабжения и канализации — по СП 73.13330.2016 до закрытия трасс; приёмо-сдаточные испытания электроустановки — по ПУЭ, гл. 1.8, с протоколом электролаборатории.
15. Осознанные отступления от ГОСТ Р 21.101-2026, принятые в комплекте: номер листа и число листов («Листов») указаны на каждом листе; на масштабных листах в основной надписи указан фактический масштаб и дан контрольный отрезок 1000 мм; развёртки стен выполнены в М 1:25 (ГОСТ 21.507-81 — 1:50…1:500) ради читаемости привязок; размерные числа и марки элементов (Д-1, ОК-1, О6) кеглем 2,5 мм, номера помещений — в кружке Ø 8 мм (канон — 3,5 мм и Ø 12 мм): так насыщенные листы А3 читаются без наложений надписей.
16. Графы «Пров.», «Н. контр.», «Утв.» основной надписи заполняются при согласовании комплекта с заказчиком; до согласования комплект подписывает автор проекта (графа «Разраб.»).

Изм.	Кол.уч	Лист	№ док.	Подп.	Дата
Разраб.		Кырлан А.С.			13.11.26
Пров.					
ГИП					
Н. контр.					
Утв.					

ГД-2026-003-АИ

Трёхкомнатная квартира

Общая площадь 78,95* м² · * размеры со скана, не замерены (реестр — л. 6–11, К-13)

Дизайн-проект интерьера трёхкомнатной квартиры

Стадия	Лист	Листов
РП	5	132

Общие данные

М б/м

Кырлан Александр Сергеевич

выпуск 13.11.2026 № 6f3a8abb2c · стр. 5 из 157

Открытые вопросы, принятые допущения и конфликты. Лист 1 из 6

Сводка по реестрам координации

Комплект предварительный по пунктам этих таблиц. Пока по пункту нет ответа или решения, показанное на указанном листе — допущение проектировщика, а не утверждённое решение.
Сводка: открытых вопросов — 27 (из них ждут факта объекта — 17: контрольного обмера, обследования или документа); изменений в реестре — 20, из них без подписи — 1.
Пункты, ответ на которые лежит на объекте, а не за столом проектировщика (графа «Вид», строка «Ждёт»), собраны на листе «Задание на контрольный обмер и обследование» (листы 12–16): что и где замерить, с какой точностью и чем подтвердить. Пункты, ждущие решения человека, на объекте не закрываются.

Открытые вопросы и принятые допущения

№	Формулировка	Вид	Кто решает	Если решения нет	Лист, где это проявляется
К-1	Ванная (2250 × 1970 мм): после утверждения стиральной машины с вертикальной загрузкой 400 × 600 мм (ИЗ-11) замечания по дверце машины и боковому зазору унитаза П2 сняты. Остаются: в зоне 750 мм перед ванной П1 стоит умывальник П3; розетка Р7 в 348 мм от стояка (нужно 500). Предложение, в проект не принято: умывальник П3 развернуть до 600 × 450 мм к стене В, унитаз П2 сдвинуть на 150 мм, розетки Р7 и Р8, светильник и зеркало перенести по новой раскладке. Решить: принять предложение, оставить как есть с открытыми замечаниями или предложить другую раскладку.	Спорно Ждёт: решения	Инженер ВК (вода, канализация)	в проекте остаются умывальник П3 в зоне перед ванной и розетка Р7 в 348 мм от стояка; эти отступления остаются открытыми	л. 48 — План выводов сантехники л. 37 — План розеток и электровыводов
К-2	Артикул плитки и калибр партии (фактический размер плитки) для ванной и санузла 2 не заданы: раскладка рассчитана по номинальным размерам — пол 600 × 600 мм, стены 600 × 1200 мм. Требование к закупке: выбрать плитку и до раскладки измерить калибр на образце партии (или взять из паспорта партии); раскладку пересчитать по измеренному калибру до заказа плитки и до укладки. Пока калибр не измерен, подрезка у стен и число плиток по листам раскладки — расчётные.	Отсутствует Ждёт: данных закупки, затем решения	Плиточник	раскладка остаётся по номинальным размерам; подрезку у стен определять по фактической партии, раскладку пересчитать по измеренному калибру	л. 62 — Раскладка плитки. Планы полов л. 64 — Раскладка плитки. Ванная. Развёртки стен л. 65 — Раскладка плитки. Санузел 2. Развёртки стен
К-3	Доли цвета по поверхностям не укладываются в схему 60/30/10 и её варианты: ведущий цвет занимает 33 % в спальне 1, 38 % в спальне 2 и 32 % в кухне-гостиной (нужно от 50 %); акцент в спальне 1 — 19 %, в спальне 2 — 18 % (больше 15 %); в гардеробной ведущий цвет занимает 90 % (больше 80 %), второй цвет почти не читается. Решить, какие поверхности считать ведущим цветом в каждой комнате, или принять распределение как есть.	Спорно Ждёт: решения	Колорист-комплектатор	цвета остаются в показанных долях, ведущий цвет в трёх комнатах не определён	л. 69 — Колерная карта
К-4	Вход в санузел 2 (с унитазом) — из кухни-гостиной: так по плану заказчика (ниша у входа на плане открыта в кухню-гостиную, в проекте закрыта перегородкой по линии низа прихожей). Вход в помещение с унитазом принято устраивать из коридора или прихожей. Принять существующее положение или перепланировать вход.	Спорно Ждёт: решения	Архитектор-планировщик	Остаётся вариант, показанный на листе; он не утверждён, лист предварительный.	л. 27 — Обмерный план л. 30 — План дверей и ведомость заполнения проёмов
К-5	Санузел 2 (1675 × 1580 мм): перед душем П6 до противоположной стены 630 мм (нужно 750); зону перед унитазом П7 и умывальником П8 занимает сам поддон душа П6; боковой зазор умывальника П8 — 150 мм (нужно 200). Принять как проектное решение «перекрытие зон движения» нельзя: VDI 6000 допускает перекрытие зон движения соседних приборов, но не прибор в зоне движения другого, а здесь в зоне стоит поддон душа, и глубина перед душем меньше 750 мм. Отступление от этой зарубежной рекомендации (в российских нормах размеры перед приборами не заданы) возможно только как осознанный отказ от неё при малом помещении либо перестановкой приборов.	Спорно Ждёт: решения	Инженер ВК (вода, канализация)	приборы остаются как показаны: поддон душа стоит в зоне перед унитазом и умывальником, глубина перед душем 630 мм; отступление не принято и не обосновано	л. 48 — План выводов сантехники
К-7	Розетки выше 1 м от пола (норма ПУЭ, п. 6.6.30 — не выше 1 м). Р7 (стиральная машина) и Р8 (фен) в ванной стояли на 1200 мм, Р33 (фен, санузел 2) — на 1100 мм: назначение не требует такой высоты, розетки опущены до 1000 мм (запись ИЗ-9). Остаются выше 1 м по назначению, основание записано в самой позиции (знак «**» у марки, примечание листа, графа «Назначение» ведомости): Р12 (ТВ над комодом, спальня 2) — 1100 мм, питание телевизора на стене, в одной зоне с ТВ2 и LAN2; Р18 (ТВ) и Р19 (ТВ-приставка, кухня-гостиная) — 1100 мм, в одной зоне с ТВ1 и LAN3; Р17 (питание слаботочного щита ЩС, прихожая) — 1700 мм, рядом со щитом на его высоте; Р25 (холодильник) — 2000 мм, над нишей М6 за съёмной панелью. Подтвердить высоты или опустить розетки.	Спорно Ждёт: решения	Инженер-электрик	высоты остаются как на листе, решение не подтверждено	л. 37 — План розеток и электровыводов л. 40, 41 — Ведомость электроточек и изделий
К-8	Проект кухни не утверждён заказчиком: выводы кухонной техники (мойка М7, посудомоечная М14, варочная панель и духовой шкаф М8, вытяжка М15, холодильник М6) приняты по типовой расстановке техники. Раскладка гарнитура принята автором проектной (ИЗ-12) с условием: до начала черновых работ сверить её и выводы техники с чертежом кухни от изготовителя гарнитура; чертёж изготовителя нужно получить и передать. Пока чертежа нет, привязки выводов даны от осей модулей гарнитура и пересматриваются вместе с проектом кухни.	Отсутствует Ждёт: документа, обмера, затем решения	Мебельщик	выводы остаются привязанными к раскладке гарнитура, принятой проектной и не сверенной с чертежом изготовителя	л. 81 — Кухня (пом. 6). Развёртка гарнитура л. 37 — План розеток и электровыводов
К-9	Гардеробная состоит из двух частей; проход между ними через стык — 280 мм (нужно 700 мм), он сужает систему хранения Г1. Принять как технический проход нельзя: по практике проектирования технический проход не уже 700 мм, меньше 600 мм — критично, а 280 мм — уже ширины плеч. Изменить границу частей либо состав Г1. Предложение исполнителя (27.10.2026): Г1 перенесена на торцевую стену А — 880 × 600 мм, штанга вдоль стены; проход по всей ширине гардеробной 880 мм, длина штанги 880 мм вместо 1700 — утвердить или выбрать иное.	Спорно Ждёт: решения	Дизайнер интерьера	проход через стык остаётся 280 мм: в часть гардеробной не пройти, пока не изменены граница частей или состав Г1	л. 32 — План расстановки мебели л. 79 — Система хранения Г1

Изм.	Кол.уч	Лист	№ док.	Подп.	Дата
Разраб.		Кырлан А.С.			13.11.26
Пров.					
ГИП					
Н. контр.					
Утв.					

ГД-2026-003-АИ

Трёхкомнатная квартира

Общая площадь 78,95* м² · * размеры со скана, не замерены (реестр — л. 6–11, К-13)

Дизайн-проект интерьера трёхкомнатной квартиры

Стадия	Лист	Листов
РП	6	132

Открытые вопросы, принятые допущения и конфликты. Лист 1 из 6
М б/м

Кырлан Александр Сергеевич

Открытые вопросы, принятые допущения и конфликты. Лист 2 из 6

Сводка по реестрам координации

Открытые вопросы и принятые допущения (продолжение)

№	Формулировка	Вид	Кто решает	Если решения нет	Лист, где это проявляется
К-11	Высота потолка 2700 мм принята: на плане заказчика она не указана. От неё зависят вертикальные размеры альбома (развёртки, шкафы, плитка, объёмы работ). Замерить высоту на объекте.	Непонятно Ждёт: обмера	Архитектор-планировщик	Остаётся значение, принятое по исходным данным; оно не подтверждено, лист предварительный.	л. 27 — Обмерный план
К-12	Две конструкции плана заказчика не определены: утолщение стены 190 × 1360 мм в гардеробной у спальни 2 (вентблок или пилон) и элемент 1470 × 160 мм на линии простенка кухни-гостиной (пилон, балка или барная стойка). Элемент 1470 × 160 мм на листах не показан, мебель от него свободна. Назначение определить на объекте.	Непонятно Ждёт: обследования	Архитектор-планировщик	Остаётся значение, принятое по исходным данным; оно не подтверждено, лист предварительный.	л. 27 — Обмерный план л. 32 — План расстановки мебели
К-13	Размеры сняты со скана плана заказчика по размерным цепочкам, контрольный обмер на объекте не выполнялся; толщины стен приняты 250 мм (наружные) и 150 мм (перегородки), на плане 85–190 мм. В двух местах принятое значение отличается от числа на плане: ширина гардеробной 1070 мм (на плане 1120 при перегородке 85 мм), ширина спальни 2 — 3130 мм (на плане 3120). Привязка стены прихожей к спальне 1 сдвинута на 40 мм относительно плана: на плане толщина стены 190 мм, в модели 150 мм (чистые размеры помещений — по плану, разница отнесена к толщинам стен). Подтвердить контрольным обмером.	Непонятно Ждёт: обмера	Архитектор-планировщик	Остаётся значение, принятое по исходным данным; оно не подтверждено, лист предварительный.	л. 27 — Обмерный план
К-14	Разрешённая мощность 15 кВт принята по типовой квартире, технических условий в материалах объекта нет; расчётная мощность 11,8 кВт. Сверить с техническими условиями.	Непонятно Ждёт: документа	Инженер-электрик	Остаётся значение, принятое по исходным данным; оно не подтверждено, лист предварительный.	л. 42 — Однолинейная схема щита
К-15	Графы «Пров.» и «Н. контр.» в штампе пусты: их заполняет человек, подписи проверяющего и нормоконтролёра разработчик проекта не ставит; для выдачи нужны подписанты, отличные от разработчика. Решение автора (ИЗ-13): графы остаются пустыми, комплект предварительный.	Отсутствует Ждёт: решения	Нормоконтролёр	графы остаются пустыми; комплект предварительный, не проверен независимо	л. 2 — Общие данные
К-16	Сдача разделов специалистами для этого проекта не оформлена (нет файлов решений по ролям). В альбоме нет листов «Пожарная безопасность» и «Звукоизоляция», программы испытаний и приёмки, допуска ГИПа. Решить, какие из этих разделов входят в состав работ; для входящих оформить сдачу.	Отсутствует Ждёт: решения	Главный инженер проекта (ГИП)	Исходных данных нет: на листе нет решения по этому пункту или оно условное; лист предварительный.	л. 2 — Общие данные
К-17	Положение стояков условно, на объекте не замерено: стояки канализации и холодной воды — в коробе Ш1 248 × 459 в углу ванной и в стене-пилоне Ш2 270 мм между санузлом 2 и кухней (по плану заказчика). От положения стояков зависят привязки выводов воды и канализации, расстояния розеток до стояка (К-1) и места люков 300 × 400. Сверить положение стояков на объекте до разметки.	Непонятно Ждёт: обмера	Инженер ВК (вода, канализация)	Остаётся значение, принятое по исходным данным; оно не подтверждено, лист предварительный.	л. 48 — План выводов сантехники л. 49 — Схема разводки водопровода и канализации
К-18	Санузел 2: ниша 1600 × 1840 мм у входа закрыта перегородкой, ниша 660 × 260 мм (уступ по плану) — фальш-стеной с рамой инсталляции: проектное решение, на плане заказчика ниша у входа открыта в кухню-гостиную. От закрытия зависят размеры санузла 2 (1675 × 1580 мм), перегородка и фальш-стена в объёмах работ. Подтвердить закрытие ниш или оставить их открытыми.	Спорно Ждёт: решения	Архитектор-планировщик	Остаётся вариант, показанный на листе; он не утверждён, лист предварительный.	л. 48 — План выводов сантехники
К-19	Модель стиральной машины П4 не выбрана. Условие закупки (решение автора проекта, ИЗ-11): вертикальная загрузка, габарит в плане 400 × 600 мм (ширина 400 мм вдоль стены Б, глубина 600 мм), высота по паспорту (в расчёте 900 мм). Машина с фронтальной загрузкой или большего габарита проекту не подходит: перед люком ванна П1, дверца не откроется. Тип загрузки и габарит до заказа сверить с паспортом выбранной модели, положение подводки — до закрытия трасс и разводки. В спецификации мебели и оборудования тот же габарит выведен по осям плана как 600 × 400 мм.	Отсутствует Ждёт: данных закупки, затем решения	Инженер ВК (вода, канализация)	машина не куплена: тип загрузки и габарит на листах условие закупки; купленная машина другого типа или габарита потребует пересмотра раскладки ванной	л. 48 — План выводов сантехники л. 56 — Спецификация сантехнического оборудования
К-20	Несущие стены не определены: проект дома и план БТИ в материалах объекта отсутствуют, тип и серия дома неизвестны, техническое заключение о несущих конструкциях не выполнялось. До заключения все существующие стены считаются несущими: демонтаж, новые проёмы и штробы в них не планируются. Нужно: запросить проект дома и поэтажный план БТИ, установить серию дома; несущие стены и допустимость вмешательства определяет техническое заключение специализированной организации.	Отсутствует Ждёт: документа, обследования	Архитектор-планировщик	Исходных данных нет: на листе нет решения по этому пункту или оно условное; лист предварительный.	л. 28 — План демонтажа и монтажа перегородок
К-21	Прямые углы помещений с кухней, санузлами, гардеробной и встроенной мебелью по скану не подтверждены: спальня 1, ванная, гардеробная, прихожая, кухня-гостиная, санузел 2. Нужен контрольный обмер: длины сторон и обе диагонали каждого помещения, отклонения углов от 90° у стен под встроенную мебель и плитку. Только после обмера в данных отмечаются прямые углы.	Отсутствует Ждёт: обмера	Архитектор-планировщик	углы принимаются прямыми по скану, не проверенными; встроенную мебель и плитку по размерам листов не заказывать до обмера	л. 27 — Обмерный план л. 32 — План расстановки мебели
К-22	Состав подрядчиков и поставщиков (кто покупает и кто монтирует радиаторы, подоконники, двери, розетки) от заказчика не получен. Принята типовая схема частного ремонта (ИЗ-14): материалы и оборудование покупает заказчик по спецификациям проекта, монтаж ведёт подрядная бригада, приёмку скрытых работ ведёт автор. Схема уточняется договором подряда: нужен договор или состав подрядчиков и поставщиков от заказчика.	Отсутствует Ждёт: решения	Прораб-координатор	остаётся типовая схема: покупает заказчик, монтирует подрядная бригада, скрытые работы принимает автор; закрепление за конкретными подрядчиками не подтверждено	л. 2 — Общие данные

						ГД-2026-003-АИ		
						Трёхкомнатная квартира Общая площадь 78,95* м² · * размеры со скана, не замерены (реестр — л. 6–11, К-13)		
Изм.	Кол.уч	Лист	№ док.	Подп.	Дата	Дизайн-проект интерьера трёхкомнатной квартиры	Стадия: РП	Лист: 7 / Листов: 132
Разраб.		Кырлан А.С.			13.11.26			
Пров.								
ГИП								
						Открытые вопросы, принятые допущения и конфликты. Лист 2 из 6 М б/м	**Кырлан Александр Сергеевич**	
Н. контр.								
Утв.								

выпуск 13.11.2026 № 6f3a8abb2c · стр. 7 из 157

Открытые вопросы, принятые допущения и конфликты. Лист 3 из 6

Сводка по реестрам координации

Открытые вопросы и принятые допущения (продолжение)

№	Формулировка	Вид	Кто решает	Если решения нет	Лист, где это проявляется
К-23	Артикулы изделий отделки не выбраны. Инженерная доска (пом. 1, 3, 4, 6, 8), керамогранит пола (пом. 2, 5, 7), керамогранит стен (пом. 2, 7), керамогранит фартука кухни (пом. 6) и плинтус МДФ (пом. 1, 3, 4, 5, 6, 8) заданы характеристиками — «аналог по характеристикам», кода изделия производителя нет. Артикул выбирается при закупке: выбрать изделия, вписать артикулы в ведомость отделки и спецификации, цвет и тон принять по образцу из партии. Количество к заказу и упаковки — расчётные, по номинальным размерам, до выбора изделия. Калибр партии плитки для ванной и санузла 2 — отдельный вопрос К-2.	Отсутствует Ждёт: данных закупки, затем решения	Отделочник	материалы остаются описанными характеристиками; заказ по спецификации и подсчёт упаковок — только после выбора изделий	л. 62 — Раскладка плитки. Планы полов л. 63 — Раскладка плитки. Прихожая. Фартук кухни л. 64 — Раскладка плитки. Ванная. Развёртки стен л. 65 — Раскладка плитки. Санузел 2. Развёртки стен л. 66 — План полов л. 67 — Ведомость отделки помещений. Лист 1 из 2 л. 70 — Спецификация отделочных материалов л. 88 — Реестр марок отделки и позиций альбома л. 120–122 — Спецификация материалов л. 123, 124 — Смета ориентировочная
К-24	Модели встраиваемой техники кухни не выбраны: холодильник (М6) и посудомоечная машина (М14) заданы описанием «аналог по характеристикам» — без производителя, серии и кода. Размеры ниш и вентзазоры взяты по типовой схеме на 60 см, а не по паспорту модели: у разных изготовителей они расходятся, и модуль, сделанный по типовой нише, может не принять выбранную технику. Нужно: выбрать модели, получить монтажные схемы изготовителей и сверить ниши модулей, вентиляцию и подключение до заказа гарнитура. Вытяжка М15 не встроена (подключение по паспорту изготовителя), но модель тоже не выбрана — выбирается вместе с остальной техникой. Проект кухни целиком — К-8.	Отсутствует Ждёт: данных закупки, затем решения	Мебельщик	ниши остаются по типовой схеме на 60 см, не подтверждённой паспортом модели; модули кухни не заказывать до выбора техники	л. 81 — Кухня (пом. 6). Развёртка гарнитура л. 83 — Кухня (пом. 6). Монтажная схема
К-25	Скрытые двери Д-2 (спальня 1 и спальня 2), Д-3 (ванная) и Д-4 (гардеробная) заданы размером проёма 800×2100 со скана плана заказчика; проёмы существующие, расширять их до технического заключения (К-20) нельзя. Скрытый блок ставят в проём с зазором 10–15 мм на сторону, а коробка занимает часть ширины, поэтому полотно получается уже проёма; размеры короба и полотна задаёт изготовитель, модель не выбрана. У Д-3 и Д-4 принятая толщина стены 150 мм, по скану плана заказчика стена 85 мм: узел скрытой двери на листе узлов показан для принятой толщины 150 мм; по замеренной толщине его пересчитать. Порядок работ один: проём замеряют в чистоте после снятия отделки, короб ставят до штукатурки, полотно навешивают после чистовой отделки стен. Дверь Д-5 стоит в проектной перегородке П-1 (К-18): её проём 700 мм принят проектом, привязка к углу 50 мм; размер короба и полотна — по выбранной модели. Нужно: замерить проёмы и толщину стены в чистоте; решить, делать полотно под существующий проём (уже проёма) или расширять проём после технического заключения; выбрать модель блока и получить размеры короба.	Непонятно Ждёт: обмера, затем решения	Архитектор-планировщик	скрытые двери не заказывать (изготовление около 30 дней): размеры короба и полотна не определены, проёмы не расширять до технического заключения; узел показан для принятой толщины стены 150 мм	л. 30 — План дверей и ведомость заполнения проёмов л. 114 — Узлы. Лист 1 из 2
К-26	Входная дверь Д-1 существующая. По плану заказчика полотно открывается наружу, в общий коридор: на плане дверей и обмерном плане дуга показана наружу, как в данных объекта. Направление открывания на объекте не проверено и не выбирается за столом. Не решено, остаётся ли существующий блок или он заменяется: в ведомости объёмов работ заложена строка «Входная дверь, поставка с монтажом и откосами». Нужно: осмотр входной двери (сторона открывания, петли, коробка, откосы) и решение автора оставить блок или заменить, и с каким открыванием.	Непонятно Ждёт: обследования, затем решения	Архитектор-планировщик	на листах дверь показана как в данных объекта (открывание наружу, существующий проём); блок для заказа не определён	л. 30 — План дверей и ведомость заполнения проёмов
К-27	Окна ОК-1…ОК-4 в проекте существующие: демонтажа и замены окон нет ни на плане демонтажа, ни в ведомости объёмов работ; ведомость заполнения проёмов фиксирует их размеры, а не заказ новых блоков. Подоконная доска и глубина откоса не заданы: откосы считаются по умолчанию (толщина стены минус коробка 70 мм), подоконники в проекте не показаны; состояние окон и подоконников не обследовано. Нужно: осмотр окон и решение — окна и подоконники остаются существующими или заменяются.	Непонятно Ждёт: обмера, затем решения	Архитектор-планировщик	окна показаны существующими, заказ оконных блоков не предусмотрен; подоконники и глубина откосов приняты, не замерены	л. 30 — План дверей и ведомость заполнения проёмов
К-28	Сроки поставки и изготовления изделий с длинной поставкой не получены ни от одного поставщика: скрытые двери Д-2…Д-5, кухонный гарнитур, встраиваемая техника, керамогранит, инженерная доска, сантехника и инсталляции, встроенная мебель по замеру цеха. В данных нет срока (срок изготовления) ни у одной позиции. Типовые диапазоны практики — скрытые двери около 30 дней, кухня и корпусная мебель 4–8 недель от замера — это ориентир, а не срок поставщика: заказывать и назначать даты по ним нельзя. Нужно: запросить у поставщиков и изготовителей срок по выбранным моделям и записать его в данные позиции.	Отсутствует Ждёт: данных закупки, затем решения	Прораб-координатор	график закупок остаётся относительным: порядок и условия есть, дат заказа нет; заказ по типовым срокам не назначается	л. 17–20 — График закупок и работ л. 123, 124 — Смета ориентировочная л. 116–119 — Ведомость объёмов работ
К-29	Климатический подрайон (СП 131.13330) не задан: принят не северный — жилые комнаты и кухня под потолком от 2,5 м (СП 54, п. 5.12); в IA, IБ, IГ, IД, IVA — от 2,7 м.	Отсутствует Ждёт: документа	Архитектор-планировщик	отметки потолков жилых — по 2,5 м; при северном подрайоне уровни ниже 2,7 м пересчитать до заказа каркаса	л. 59 — План потолков

Изм.	Кол.уч	Лист	№ док.	Подп.	Дата	ГД-2026-003-АИ			
						Трёхкомнатная квартира Общая площадь 78,95* м² · * размеры со скана, не замерены (реестр — л. 6–11, К-13)			
Разраб.		Кырлан А.С.			13.11.26	Дизайн-проект интерьера трёхкомнатной квартиры	Стадия	Лист	Листов
Пров.							РП	8	132
ГИП									
						Открытые вопросы, принятые допущения и конфликты. Лист 3 из 6 М б/м	**Кырлан Александр Сергеевич**		
Н. контр.									
Утв.									

выпуск 13.11.2026 № 6f3a8abb2c · стр. 8 из 157

Открытые вопросы, принятые допущения и конфликты. Лист 4 из 6

Сводка по реестрам координации

Изменения проекта после выпуска листов (реестр изменений)

№	Дата	Лист	Было	Стало	Кто решил, подпись
ИЗ-1	05.10.2026	л. 48 — План выводов сантехники л. 37 — План розеток и электровыводов л. 56 — Спецификация сантехнического оборудования	В ванной и санузле 2 приборов отопления не было.	Добавлены электрические полотенцесушители IP44: П10 в ванной (480 мм, низ 900 мм) и П13 в санузле 2 (400 мм, низ 900 мм), выводы ЭВ6 и ЭВ7; мощность группы 13 — 2,4 кВт вместо 1,8 кВт. Основание: (в ванной и санузле есть полотенцесушитель — он же прибор отопления мокрой зоны); водяной не взят: стояка горячей воды в данных объекта нет, взят электрический IP44. Решение исполнителя: П10, П13, ЭВ6 и ЭВ7 остаются со знаком «**» (автором не подтверждены).	Утверждено: исполнитель по поручению Кырлана А.С., 05.10.2026. Предложил: исполнитель.
ИЗ-2	05.10.2026	л. 66 — План полов л. 67 — Ведомость отделки помещений. Лист 1 из 2	Ванная и санузел 2: пирог пола — стяжка 50 мм, слоя гидроизоляции в пироге не было.	Стяжка 33 мм и слой обмазочной гидроизоляции 2 мм (2 слоя, заведение на стены 200 мм); верх плиты — вровень с остальными помещениями. Основание: (в мокром помещении в пироге пола есть слой гидроизоляции с толщиной). Знак «**» у пола ванной и санузла 2 остаётся: решение исполнителя автором не подтверждено.	Утверждено: исполнитель по поручению Кырлана А.С., 05.10.2026. Предложил: исполнитель.
ИЗ-3	05.10.2026	л. 39 — План выключателей и схема включения л. 57 — Техническое задание на подбор светильников	Кухня-гостиная: подвесы над столом (L14) и подсветка столешницы (L16) без светорегулятора, сценарии «Вечер» 50 % и «Ужин» 30 % недостижимы.	В выключателях S11 и S12 добавлены светорегуляторы (тип te); светильники Св42–Св44, лента подсветки и блок питания БП5 приняты диммируемыми. Основание: (промежуточный уровень сценария — только группе на светорегуляторе). Знак «**» у S11, S12, Св42–Св44 и БП5 остаётся.	Утверждено: исполнитель по поручению Кырлана А.С., 05.10.2026. Предложил: исполнитель.
ИЗ-4	05.10.2026	л. 37 — План розеток и электровыводов л. 110 — Развёртки стен А, Б. Санузел 2 (пом. 7)	Розетка Р33 (фен, санузел 2) на высоте 1200 мм, в перекрестье швов плитки.	Розетка Р33 на высоте 1100 мм, вне шва плитки. Затем высота снижена до 1000 мм вместе с Р7 и Р8 — запись ИЗ-9. Основание: (розетка — в центре плитки или на шве, не в перекрестье швов).	Утверждено: исполнитель по поручению Кырлана А.С., 05.10.2026. Предложил: исполнитель.
ИЗ-5	05.10.2026	л. 77 — Встроенная мебель. Схема расположения л. 81 — Кухня (пом. 6). Развёртка гарнитура	Кухня-гостиная: вывод «вытяжка» был, самой вытяжки в мебели не было; холодильник М6 описан только нишей.	Добавлена вытяжка над варочной панелью М15 (600 × 400 × 600 мм, низ 1600 мм); холодильник М6 описан как встраиваемый 60 см с вентзазорами в цоколе и под карнизом. Основание: (под вывод «вытяжка» и «холодильник» в помещении должна стоять сама техника). Знак «**» у М15 и М6 остаётся; проект кухни заказчиком не утверждён (К-8).	Утверждено: исполнитель по поручению Кырлана А.С., 05.10.2026. Предложил: исполнитель.
ИЗ-6	05.10.2026	л. 32 — План расстановки мебели л. 69 — Колерная карта	Марки: кухня К1…К14, шкафы П5 и П9, декор Д1…Д9.	Марки: мебель М (кухня М1…М14, шкафы М16 и М17), декор ДК1…ДК9; у полотенцесушителя санузла 2 — П13, потому что П11 занят мойкой. Позиции не менялись. В поле проверка света образцов «D65 и лампа проекта» заменено на «D65, лампа проекта» (смысл прежний: два источника сличения).	Утверждено: Кырлан А.С., 12.11.2026. Предложил: исполнитель.
ИЗ-7	05.10.2026	л. 80 — Шкаф-купе М16 л. 85 — Шкафы. Монтажная схема	Шкаф-купе (П5, ныне М16) 2600×600 мм: способ сборки не задан; диагональ боковины 2668 мм больше высоты до потолка 2620 мм.	Задана сборка стоя на месте (сборка: in-place): готовый корпус не поднять. Решение подтверждено автором 05.10.2026 (вопрос К-10 закрыт): размер корпуса не меняется, готовый корпус не поднять — сборка стоя на месте.	Утверждено: Кырлан А.С., автор проекта, 05.10.2026. Предложил: решение автора проекта, оформлено исполнителем по его поручению (запись внесена разработчиком по замечанию проверки).
ИЗ-8	05.10.2026	л. 37 — План розеток и электровыводов л. 40, 41 — Ведомость электроточек и изделий	В ванной и санузле 2 не было вывода к вентилятору вытяжки и коробки уравнивания потенциалов.	Добавлены выводы к вентиляторам: ЭВ4 (ВР1, ванная) и ЭВ5 (ВР3, санузел 2) — группа 3, высота 2389 мм, включение с основным светом, таймер выбега в вентиляторе; и коробки уравнивания потенциалов КУП1 (ванная) и КУП2 (санузел 2) — высота 300 мм, у входа, вне зон 0–2, проводник от шины PE щита ЩК, сечение — по проекту ЭОМ. Основание: правила проверки (питание вентилятора вытяжки мокрого помещения) и (КУП в помещении с ванной или душем). Заказчик эти позиции не заказывал; решение исполнителя, ЭВ4, ЭВ5, КУП1 и КУП2 остаются со знаком «**» (автором поштучно не утверждены).	Утверждено: исполнитель по поручению Кырлана А.С., 05.10.2026. Предложил: исполнитель.
ИЗ-9	05.10.2026	л. 37 — План розеток и электровыводов л. 40, 41 — Ведомость электроточек и изделий	Розетки Р7 (стиральная машина) и Р8 (фен) в ванной — 1200 мм, Р33 (фен, санузел 2) — 1100 мм, с флагом решения: высота не обоснована назначением.	Р7, Р8 и Р33 на высоте 1000 мм — верхний предел нормы (ПУЭ, п. 6.6.30, не выше 1 м); флаг решения снят. Назначение стиральной машины и фена не требует большей высоты. Р12, Р17, Р18, Р19 и Р25 остались выше 1 м по назначению (решение исполнителя; основание записано в самой позиции, вопрос К-7): Р12, Р18 и Р19 — 1100 мм, в одной зоне с выводами ТВ и LAN, которые тоже на 1100 мм; Р17 — 1700 мм, рядом с ЩС на высоте щита (1700 мм); Р25 — 2000 мм, над нишей М6 за съёмной панелью с доступом, как и БП5. Высоты Р7, Р8, Р33 и всех перечисленных автором поштучно не подтверждены, знак «**» у них остаётся.	Утверждено: исполнитель по поручению Кырлана А.С., 05.10.2026. Предложил: исполнитель.

Изм.	Кол.уч	Лист	№ док.	Подп.	Дата
Разраб.		Кырлан А.С.			13.11.26
Пров.					
ГИП					
Н. контр.					
Утв.					

ГД-2026-003-АИ

Трёхкомнатная квартира

Общая площадь 78,95* м² · * размеры со скана, не замерены (реестр — л. 6–11, К-13)

Дизайн-проект интерьера трёхкомнатной квартиры

Стадия	Лист	Листов
РП	9	132

Открытые вопросы, принятые допущения и конфликты. Лист 4 из 6

М б/м

Кырлан Александр Сергеевич

Открытые вопросы, принятые допущения и конфликты. Лист 5 из 6

Сводка по реестрам координации

Изменения проекта после выпуска листов (реестр изменений) (продолжение)

№	Дата	Лист	Было	Стало	Кто решил, подпись
ИЗ-10	05.10.2026	л. 37 — План розеток и электровыводов л. 40, 41 — Ведомость электроточек и изделий	Розетки Р7 (стиральная машина) и Р8 (фен) в ванной, Р33 (фен) в санузле 2 стояли в зоне 3 по ПУЭ, но ближе 2,5 м от границы зоны 1 по британской норме BS 7671 (п. 701.512.3); какая норма принята — вопрос К-6.	Принята норма ПУЭ (п. 7.1.48): розетки в зоне 3 помещения с ванной или душем допустимы при защите УЗО 30 мА. Положение розеток не менялось. Основание: розетки вне зон 0–2 (до границы зоны 1: Р7 — 650 мм, Р8 — 1220 мм, Р33 — 800 мм), исполнение IP44, группы 12 и 13 защищены УЗО 30 мА типа А. Это сознательное отступление от зарубежной нормы BS 7671: в России она не действует, по ней в таком месте допустима только бритвенная розетка с разделительным трансформатором. Высота розеток — отдельный вопрос К-7.	Утверждено: Кырлан А.С., автор проекта, 05.10.2026. Предложил: решение автора проекта, оформлено исполнителем по его поручению.
ИЗ-11	05.10.2026	л. 48 — План выводов сантехники л. 56 — Спецификация сантехнического оборудования л. 37 — План розеток и электровыводов л. 33–36 — Спецификация мебели и оборудования	Ванная: стиральная машина П4 фронтальной загрузки 600 × 600 мм, габарит условный (модель не выбрана); перед люком ванна П1, свободно 50 мм вместо 500 — дверца не откроется (вопросы К-1, К-19).	Утверждена стиральная машина с вертикальной загрузкой, габарит в плане 400 × 600 мм (ширина 400 вдоль стены Б, глубина 600). На плане П4 уменьшена с 600 × 600 до 400 × 600, место у стены Б прежнее (500 мм от стены А), розетка Р7 остаётся на стене Б у машины. Габарит и тип загрузки — условие закупки, а не пожелание: машина с фронтальной загрузкой или большего габарита проекту не подходит (перед люком ванна П1). Условие записано в спецификации сантехнического оборудования, на листе выводов сантехники и в вопросе К-19 (задание на закупку). Модель по-прежнему не выбрана: габарит и подводку сверить по паспорту до закрытия трасс. Спецификация мебели и оборудования выводит габарит машины по осям плана — 600 × 400 мм: это тот же размер (глубина 600 в комнату, ширина 400 вдоль стены).	Утверждено: Кырлан А.С., автор проекта, 05.10.2026. Предложил: решение автора проекта, оформлено исполнителем по его поручению.
ИЗ-12	05.10.2026	л. 81 — Кухня (пом. 6). Развёртка гарнитура л. 37 — План розеток и электровыводов л. 33–36 — Спецификация мебели и оборудования	Кухня-гостиная: раскладка гарнитура и выводы техники приняты по типовой расстановке, проект кухни не утверждён (вопрос К-8).	Раскладка гарнитура принята проектной: мойка М7 у шахты Ш2, посудомоечная М14 рядом с мойкой, варочная панель и духовой шкаф в М8, вытяжка М15, холодильник М6. Условие: до начала черновых работ сверить раскладку и выводы техники с чертежом кухни от изготовителя; расхождения вносятся в реестр изменений, выводы пересматриваются по его чертежу. Проект кухни остаётся неутверждённым до этой сверки: позиции М7 и М8 сохраняют знак «*», примечание о выводах кухонной техники на листах сохранено, вопрос К-8 открыт.	Утверждено: Кырлан А.С., автор проекта, 05.10.2026. Предложил: решение автора проекта, оформлено исполнителем по его поручению.
ИЗ-13	05.10.2026	л. 2 — Общие данные	Графы «Пров.» и «Н. контр.» основной надписи пусты (вопрос К-15); как с ними поступать — не записано.	Графы «Пров.» и «Н. контр.» остаются пустыми: независимой проверки и нормоконтроля проекта не было, автор проекта сам себе их не подписывает. Комплект выпускается предварительным: пока нет подписи проверяющего и нормоконтролёра, отличных от разработчика, он не считается окончательным.	Утверждено: Кырлан А.С., автор проекта, 05.10.2026. Предложил: решение автора проекта, оформлено исполнителем по его поручению.
ИЗ-14	05.10.2026	л. 2 — Общие данные	Матрицы ответственности (делает / поставляет / принимает / хранит) нет; кто покупает и кто монтирует — не определено.	Принята типовая схема частного ремонта: материалы и оборудование покупает заказчик по спецификациям проекта; монтаж ведёт подрядная бригада; приёмку скрытых работ ведёт автор проекта; хранение — по договору подряда. Распределение закреплено по радиаторам, подоконникам, дверям и коробам скрытых дверей, розеткам и выключателям, сантехническим приборам, светильникам, отделочным материалам и плитке. Это схема по умолчанию, не факт: состав подрядчиков и поставщиков от заказчика не получен (вопрос К-22), схема уточняется договором подряда.	Утверждено: Кырлан А.С., 12.11.2026. Предложил: исполнитель.
ИЗ-15	05.10.2026	л. 37 — План розеток и электровыводов л. 40, 41 — Ведомость электроточек и изделий	Розетка Р7 (стиральная машина, ванная) на стене Б со смещением 685 мм: 348 мм от стояка холодной воды Ст В1-1 при практике приёмки не ближе 500 мм.	Р7 на стене Б со смещением 985 мм (на 300 мм дальше вдоль стены, по-прежнему у стиральной машины П4; высота 1000 мм прежняя): до стояка Ст В1-1 644 мм. Новое место — на шве плитки. Расстояние Р7 до границы зоны 1 стало 691 мм вместо 650 мм, названных в ИЗ-10; принятая там норма ПУЭ и положение Р8 и Р33 не затронуты. Положение стояков условно (К-17): отступ сделан от принятого положения, не от замера. Решение исполнителя; знак «**» у Р7 остаётся (высота вопрос К-7).	Утверждено: Кырлан А.С., 12.11.2026. Предложил: исполнитель.
ИЗ-16	06.10.2026	л. 48 — План выводов сантехники л. 49 — Схема разводки водопровода и канализации л. 56 — Спецификация сантехнического оборудования л. 114 — Узлы. Лист 1 из 2	Короб стояков Ш1 в углу ванной: в данных 180 × 450 мм (х 7890), на листе узлов 248 × 459 мм. Стояк канализации Ø110 с изоляцией 20 мм и просветом 40 мм до стенки в 180 мм не помещается: размер не годился ни как внутренний, ни как наружный. Стиральная машина П4 стояла в 50 мм от короба (у 500).	Один источник габарита: внутренний 195 × 406 мм (трубы Ст К1-1 Ø110 и Ст В1-1 Ø32, изоляция 20 мм, просвет 40 мм, считая от стен угла), обшивка 53 мм (профиль 28 + ГКЛВ 2 × 12,5) на свободных сторонах, наружный габарит каркаса 248 × 459 мм; короб остаётся в углу у стен (х 7822, у 0). Облицовка плиткой — сверх наружного габарита. Стиральная машина П4 сдвинута на 10 мм (у 510) — зазор до короба 51 мм при требовании не менее 50 мм. Положение стояков по-прежнему условно (К-17), размер короба пересчитывается по замеру. Решение исполнителя; знак «*» у стояков Ст К1-1 и Ст В1-1 (от них — положение и размер короба, К-17) и у машины П4 остаётся: автор их поштучно не утверждал.	Утверждено: Кырлан А.С., 12.11.2026. Предложил: исполнитель.

Изм.	Кол.уч	Лист	№ док.	Подп.	Дата	ГД-2026-003-АИ			
						Трёхкомнатная квартира Общая площадь 78,95* м² · * размеры со скана, не замерены (реестр — л. 6–11, К-13)			
Разраб.		Кырлан А.С.			13.11.26	Дизайн-проект интерьера трёхкомнатной квартиры	Стадия	Лист	Листов
Пров.							РП	10	132
ГИП									
						Открытые вопросы, принятые допущения и конфликты. Лист 5 из 6 М б/м	**Кырлан Александр Сергеевич**		
Н. контр.									
Утв.									

выпуск 13.11.2026 № 6f3a8abb2c · стр. 10 из 157

Открытые вопросы, принятые допущения и конфликты. Лист 6 из 6

Сводка по реестрам координации

Изменения проекта после выпуска листов (реестр изменений) (продолжение)

№	Дата	Лист	Было	Стало	Кто решил, подпись
ИЗ-17	06.10.2026	л. 45 — План слаботочных сетей л. 43 — План принципиальных трасс	Состав и места слаботочки в данных проекта заданы проектировщиком: щит слаботочный ЩС, точки доступа Wi-Fi AP1 и AP2. План заказчика их не содержит, подтверждения заказчика в данных нет.	Слаботочка остаётся предложением проектировщика, заказчиком не утверждена: щит слаботочный ЩС в Прихожей (стена Г, 3350 мм от угла, высота 1700 мм, рядом со щитом ЩК; ввод оптики, ONT, роутер, патч-панель), точка доступа AP1 в Прихожей (потолок, x 6800, y 6300) и точка доступа AP2 в Кухне-гостиной (потолок, x 12000, y 5500), питание PoE, кабель U/UTP кат. 6. Основание: (если заданы слаботочные точки, задан и слаботочный щит, к которому они сходятся); число и места точек доступа — ориентир практики «одна на 40–60 м²». Заказчик состав и места слаботочки не задавал и не подтверждал: решение исполнителя, знак «**» у ЩС, AP1 и AP2 остаётся до утверждения автором; число и места точек доступа проверить по замеру уровня сигнала после монтажа.	Утверждено: Кырлан А.С., 12.11.2026. Предложил: исполнитель.
ИЗ-18	30.10.2026	л. 81 — Кухня (пом. 6). Развёртка гарнитура л. 83 — Кухня (пом. 6). Монтажная схема л. 106 — Развёртка стены В1. Кухня-гостиная (пом. 6), кухонный фронт л. 30 — План дверей и ведомость заполнения проёмов л. 48 — План выводов сантехники л. 32 — План расстановки мебели	Кухонный ряд М6…М8 3800 мм посажен от черновой грани стены Б при чистовой длине стены 3770; дверь Д-5 с простенком 50 мм до шахты Ш2; мойка П11 500×450 против выреза 700×480; ТВ в спальне 2 только точками ЭОМ.	М8 — 1775 (ряд 3775, зазор 10 мм до чистовой грани под компенсатор); Д-5 — смещение 825 (простенок 150); П11 — 700×480 по вырезу М7; в спальне 2 добавлен ТВ С12 на кронштейне над комодом С10. Знак «**» у Д-5 и С12 до подписи автора.	Утверждено: Кырлан А.С., 12.11.2026. Предложил: исполнитель.
ИЗ-19	10.11.2026	л. 37 — План розеток и электровыводов л. 45 — План слаботочных сетей л. 32 — План расстановки мебели	ТВ2 и LAN2 на стене С со смещением 2135 и 2285 мм, высота 1100 мм — за телевизором С12 (смещение 1835…3035, 1000…1700 мм от пола): точки закрыты мебелью.	ТВ2 — смещение 3200 мм, LAN2 — 3350 мм на стене С (было 2135 и 2285), высота 1100 мм прежняя: выводы вынесены вправо за габарит телевизора С12 (его правый край 3035 мм), зазор до телевизора 165 и 315 мм, до угла не менее 815 мм; кабель в телевизор идёт по стене сбоку от кронштейна. Розетка Р12 (1985 мм, высота 1100 мм, «доступ сбоку») и телевизор С12 не тронуты. Сам телевизор остаётся предложением (ИЗ-18, К-7).	Утверждено: Кырлан А.С., 12.11.2026. Предложил: исполнитель.
ИЗ-20	12.11.2026	л. 72 — План текстиля и декора л. 74 — Ведомость текстиля л. 75 — Ведомость декора	Разбор двух критиков по кадрам: «стерильный шоурум, жизни нет»; ванна П1 в кадре без смесителя — в данных у прибора не было ни наименования, ни модели. Санузлы без текстиля и предметов; прихожая и коридор — голые стены; на столах, тумбах и комоде нет ни одной вещи; в спальне 1 нет зеркала; на диване и кроватях по 5 декоративных подушек.	Ванна П1 — «акриловая 1600×750, смеситель настенный». Ванная: банные и ручные полотенца на полотенцесушителе П10 (Т20, Т21), коврик 800×450 у бортика ванны (Т22; вне проёма Д-3), ваза с сухой веткой и свеча с диффузором на полке короба инсталляции (ДК10, ДК11). Санузел 2: полотенца на П13 (Т23, Т24), ваза с сухоцветом на полке короба (ДК12). Прихожая: ковёр-дорожка 700×2000 вдоль шкафа-купе (Т25; проход между шкафом М16 и банкеткой М17, вне полотна входной двери), графика 350×500 на стене Г между шкафом и щитом (ДК13). Коридор: акварель 800×600 на стене В (ДК14; глубина коридора 1160 — только настенный декор). Спальня 1: зеркало в рост на стене В (ДК15), сансевиерия в глубине комнаты (ДК16; до окна 4,6 м — теневыносливое растение), книги и свеча на тумбе С2 (ДК17), настольная лампа на столе С4 (ДК18). Спальня 2: керамика на комоде С10 слева от экрана (ДК19), замиокулькас (ДК20), книги на тумбе С8 (ДК21). Кухня-гостиная: книги и свеча на журнальном столе (ДК22), керамика на тумбе М18 (ДК23), пастель над креслом на стене А (ДК24), керамика на столешнице кухни (ДК25). Декоративных подушек — по 4 на диван и кровати (Т4, Т10, Т17: 3 → 2). Цвета — из палитры проекта: дымчатый зелёный Green Smoke, сине-зелёный Hague Blue, грейж Pumice, белый Winter. Знак «**» у позиций до подписи автора.	Не утверждено: подписи нет. решение исполнителя; предложение проектировщика, на утверждение А. С. Кырлана

Примечания

1. Номера листов — по ведомости рабочих чертежей комплекта (лист «Общие данные»).
2. Графа «Если решения нет» показывает состояние решения на листах; влияние на сроки и стоимость по пунктам не оценивалось.
3. Пункт, по которому принято решение, при следующем выпуске комплекта из таблиц исключается.

Изм.	Кол.уч	Лист	№ док.	Подп.	Дата
Разраб.		Кырлан А.С.			13.11.26
Пров.					
ГИП					
Н. контр.					
Утв.					

ГД-2026-003-АИ

Трёхкомнатная квартира

Общая площадь 78,95* м² · * размеры со скана, не замерены (реестр — л. 6–11, К-13)

Дизайн-проект интерьера трёхкомнатной квартиры

Стадия	Лист	Листов
РП	11	132

Открытые вопросы, принятые допущения и конфликты. Лист 6 из 6

М б/м

Кырлан Александр Сергеевич

выпуск 13.11.2026 № 6f3a8abb2c · стр. 11 из 157

Задание на контрольный обмер и обследование. Лист 1 из 5

ПРЕДВАРИТЕЛЬНО · не для производства работ · открыто пунктов: 28 (реестр — л. 6–11)

Что замерить, вскрыть и получить до заказа материалов и изделий

Задание собрано из открытых вопросов, ответ на которые лежит на объекте или в документах, а не за столом проектировщика. Пока факт не получен, размер, материал или положение на листах — допущение (знак «*»), а не замер.
Сводка: на объекте — 18 (до демонтажа — 16; после демонтажа — 1; после черновых работ — 1); документом и при закупке — 10; из допущений в данных и на листах — 19, из них без вопроса в реестре — 4. Закрываются вопросы: К-2, К-8, К-11–К-14, К-17–К-21, К-23–К-29 (18). Вопросы, ждущие решения человека, задание не закрывает — они решаются по реестру открытых вопросов.

Условия проведения

Порядок работ	Приёмы и точность	Кто присутствует	Если факт не совпал с проектом
1. До демонтажа — существующее состояние: контур, диагонали, высоты, проёмы, оси стояков, ниши и конструкции, которые видны. 2. После демонтажа, до черновых работ — то, что закрывали отделка и короба: основание стен, фактические толщины, углы, узлы. 3. После черновых работ, до чистового пола — габариты кухни и встроенной мебели по готовым стенам: после штукатурки и выравнивания размеры отличаются от размеров до работ. 4. Документы и данные закупки — не на объекте: к сроку из последней таблицы, от них зависят привязки и заказ. Что заказывается по размеру из задания, до закрытия пункта не заказывают: сроки изготовления — по графику закупок прораба.	Обход по часовой стрелке от входа: стены, проёмы, потолок, коммуникации (стояки, щиток, вентканалы), особенности (ниши, короба, выступы). Размеры записывают в мм; сумма участков равна общему размеру, при цепочке длиннее трёх участков ставят проверочный (общий) размер. Диагонали каждого помещения; если две диагонали различаются на 5 мм и больше, разницу подписывают на плане. Потолок — в нескольких точках: центр, углы, у проёмов. Проём — ширина, высота, глубина откоса, привязка к ближайшим углам, высота подоконника. Допустимая погрешность прибора — 2–3 мм на метр; размеры округляют кратно 5 мм; два контрольных промера одного размера не должны расходиться более чем на 2 %. Допуск по пункту — в графе «Точность». План БТИ обмер не заменяет.	Прораб (отвечает за проведение) — назначает день и порядок обхода, открывает объект и освобождает помещения, ведёт это задание и реестр изменений. Архитектор — выполняет обмер, составляет акт контрольного обмера и подписывает результаты по размерам и конструкциям. Владельцы вопросов присутствуют при пунктах своего раздела или принимают результат до заказа: Плиточник — К-2; Мебельщик — К-8, К-24; Инженер-электрик — К-14; позиции О-1; Инженер ВК (вода, канализация) К-17, К-19; Отделочник — К-23; позиции О-17; Прораб-координатор — К-28; Инженер ОВ — позиции О-2, О-3. Технадзор — при вскрытиях и обследованиях: фото с рулеткой до закрытия. Заказчик или его представитель — передаёт документы (план БТИ, проект дома, технические условия, паспорта), подписывает акт. Проектных решений на обмере не принимают: обмер даёт факт, решения — по реестру открытых вопросов (листы 6–11).	1. В пределах допуска пункта — принимается измеренное значение, лист перевыпускается, знак «*» снимается. 2. Больше допуска или контрольные промеры расходятся более чем на 2 % — промер повторяют; не подтвердилось — запись в реестр изменений (дата, лист, было, стало, кто решил, подпись), работы в этом месте не начинают. 3. Затронуты несущая стена, стояк, вентканал или мокрая зона — сразу владельцу раздела и ГИПу (главному инженеру проекта); между разделами не больше двух кругов, затем решает ГИП. 4. На объекте устно ничего не согласуется: каждое решение — записью в реестр с подписью.

Этап 1. До демонтажа

№	Где	Способ	Что сделать	Кто выполняет	Точность	Что пересчитается в альбоме	Чем подтверждается	Закрывает вопросы реестра
О-1	Вход в квартиру или лестничная клетка; место щита на плане	Обмер	Существующий щиток и счётчик электроэнергии: место и габарит ниши, состояние ввода, марка и сечение вводного кабеля, наличие вводного автомата и УЗО, пломбы.	Архитектор	±5 мм	Ниша и место щита на листах; вводной кабель и аппараты на однолинейной схеме; расстояния до первых групп. Листы: л. 42 — Однолинейная схема щита	акт контрольного обмера; фото с рулеткой и привязкой к стене или углу	Вопроса в реестре нет: Альбом принимает щит и ввод без осмотра. Результат принимает: Инженер-электрик
О-2	Спальня 1 (пом. 1), Спальня 2 (пом. 4), Кухня-гостиная (пом. 6); у окон	Обмер	Положение стояков отопления (подающий и обратный) от граней стен, диаметры, наличие запорной арматуры; существующие радиаторы: число секций, межосевое расстояние, подводки. В данных стояков отопления нет — лист отопления выводит их условно у откоса окна, радиаторы — «принципиально, по расчёту».	Архитектор	±5 мм	План отопления: места стояков и подводок, привязки радиаторов; подбор радиаторов по теплотехническому расчёту; радиаторы и узлы подключения в ВОР и спецификации. Листы: л. 47 — План отопления	акт контрольного обмера; фото с рулеткой и привязкой к стене или углу	Вопроса в реестре нет: Альбом принимает положение стояков и радиаторов отопления без обмера. Результат принимает: Инженер ОВ
О-3	Ванная (пом. 2), Кухня-гостиная (пом. 6), Санузел 2 (пом. 7)	Обмер	Положение и сечение вентканалов кухни и санузлов, проверка тяги (по листку бумаги или анемометром), состояние решёток. В данных каналов нет: лист вентиляции ставит решётки и вход вытяжки у стояков по практике.	Архитектор	±5 мм	План вентиляции: места решёток и вход вытяжки; воздухообмен по помещениям; каналы не сужать и не закрывать (Постановление Госстроя № 170, п. 1.7.2). Листы: л. 46 — План вентиляции	акт контрольного обмера; фото с рулеткой и привязкой к стене или углу	Вопроса в реестре нет: Альбом ставит вентиляционные выводы без обмера каналов. Результат принимает: Инженер ОВ

Допущения и предложения на листе
Основа листа: размеры сняты со скана плана заказчика по размерным цепочкам, контрольный обмер на объекте не выполнялся (К-13); высота потолка 2700 мм принята: на плане заказчика не указана (К-11); толщины стен приняты: наружные 250 мм, перегородки 150 мм (на плане 85–190 мм) (К-13); разрешённая мощность 15 кВт принята по типовой квартире, технических условий нет (К-14); утолщение стены 190 × 1360 мм и элемент 1470 × 160 мм плана заказчика не определены (К-12); ниши санузла 2 закрыты перегородкой и фальш-стеной: проектное решение, на плане заказчика ниша у входа открыта (К-18); несущие стены не определены: до технического заключения все существующие стены считаются несущими (К-20); окна существующие и сохраняются; подоконная доска и глубина откосов не заданы — приняты, не замерены (К-27); подрайон климата не задан — принят не северный (жилые от 2,5 м) (К-29).
См. лист открытых вопросов (лист 7, записи К-11–К-14, К-18, К-20; лист 8, записи К-27, К-29).

Изм.	Кол.уч	Лист	№ док.	Подп.	Дата
Разраб.		Кырлан А.С.			13.11.26
Пров.					
ГИП					
Н. контр.					
Утв.					

ГД-2026-003-АИ

Трёхкомнатная квартира

Общая площадь 78,95* м² · * размеры со скана, не замерены (реестр — л. 6–11, К-13)

Дизайн-проект интерьера трёхкомнатной квартиры

Стадия	Лист	Листов
РП	12	132

Задание на контрольный обмер и обследование.
Лист 1 из 5
М б/м

Кырлан Александр Сергеевич

выпуск 13.11.2026 № 6f3a8abb2c · стр. 12 из 157

Задание на контрольный обмер и обследование. Лист 2 из 5

Что замерить, вскрыть и получить до заказа материалов и изделий

Этап 1. До демонтажа (продолжение)

№	Где	Способ	Что сделать	Кто выполняет	Точность	Что пересчитается в альбоме	Чем подтверждается	Закрывает вопросы реестра
О-4	Все помещения квартиры	Обмер	Высота потолка в каждом помещении в нескольких точках: центр, углы, у проёмов. Принято 2700 мм: на плане заказчика не указана.	Архитектор	±5 мм	Вертикальные размеры альбома: развёртки, шкафы, плитка, объёмы работ; сборка шкафа-купе М16 (диагональ боковины 2668 мм против 2620 мм до потолка). Листы: л. 27 — Обмерный план	акт контрольного обмера	К-11 Результат принимает: Архитектор
О-5	Гардеробная у спальни 2 (утолщение стены); кухня-гостиная, линия простенка (элемент 1470 × 160 мм)	Обследование	Определить назначение двух конструкций плана заказчика: утолщение стены 190 × 1360 мм (вентблок или пилон) и элемент 1470 × 160 мм (пилон, балка или барная стойка).	Архитектор	размеры ±5 мм	Показ элемента 1470 × 160 мм на листах (сейчас не показан, мебель от него свободна); обмерный план и план расстановки мебели. Листы: л. 27 — Обмерный план л. 32 — План расстановки мебели	фото с рулеткой и привязкой к стене или углу; акт контрольного обмера	К-12 Результат принимает: Архитектор
О-6	Вся квартира, все помещения; обход по часовой стрелке от входа	Обмер	Контрольный обмер всех помещений: чистые размеры по размерным цепочкам, толщины стен (приняты 250 мм наружные и 150 мм перегородки, на плане 85–190 мм), диагонали. Отдельно проверить места, где принятое значение отличается от плана: ширина гардеробной 1070 мм (на плане 1120), ширина спальни 2 — 3130 мм (на плане 3120), привязка стены прихожей к спальне 1 (на плане стена 190 мм, в модели 150 мм).	Архитектор	±5 мм; диагонали — разница от 5 мм подписывается	Чистые размеры и площади помещений, толщины стен; размеры, по которым заказываются материалы и изделия. Листы: л. 27 — Обмерный план	акт контрольного обмера	К-13, К-18 Результат принимает: Архитектор
О-7	Все помещения; пол вскрыть до плиты в контрольных точках после снятия покрытий	Обмер	Нивелировка: отметка существующего пола и верха плиты перекрытия в каждом помещении и у порога входной двери — от одной сквозной отметки (нивелир или лазерный уровень). Верх плиты принят расчётом по пирогу пола (−0,064 от чистого пола), существующий пол в проекте не привязан.	Архитектор	±5 мм; перепад плиты между помещениями размером на плане	Отметки ±0,000, −0,015 и −0,064; толщины стяжки по помещениям, объёмы стяжки и демонтажа пола. Листы: л. 27 — Обмерный план	акт контрольного обмера	К-13 Результат принимает: Архитектор
О-8	Ванная (пом. 2), короб Ш1 248 × 459 мм: Ст К1-1*, Ст В1-1*; квартира, короб Ш2 270 × 1840 мм: Ст К1-2*, Ст В1-2*; наличие стояка ГВС, арматуры и счётчиков — по всей квартире	Обмер	Положение стояков Ст К1-1*, Ст В1-1*, Ст К1-2*, Ст В1-2*: привязка осей от граней стен, диаметры, размеры короба и люков. Стояк горячей воды Т3 в данных не задан, на листах ВК принят рядом с Ст В1-1*, Ст В1-2*: выяснить, есть ли он в доме, и где. Отключающая арматура и счётчики воды на вводах: положение, тип, пломбы управляющей компании. Сверить до разметки выводов.	Архитектор	±5 мм	Привязки выводов воды и канализации на планах выводов и разводки; расстояние розеток до стояка; места люков 300 × 400 мм; трассы Т3 и полотенцесушители (водяной или электрический); узлы ввода в спецификации ВК (краны, фильтры, счётчики). Привязки выводов воды и канализации; расстояние розеток до стояка (К-1); места люков 300 × 400 мм. Листы: л. 48 — План выводов сантехники л. 49 — Схема разводки водопровода и канализации	акт контрольного обмера; фото с рулеткой и привязкой к стене или углу	К-17 Результат принимает: Инженер ВК (вода, канализация)
О-9	Все стены квартиры; специализированная организация либо конструктор по проекту дома	Обследование	Какие участки стен несущие: техническое заключение по результатам обследования.	Конструктор или специализированная организация	по заключению организации	Разметка несущих и ненесущих стен на обмерном плане и плане демонтажа; допустимость демонтажа, проёмов и штроб (пока все стены считаются несущими). Листы: л. 28 — План демонтажа и монтажа перегородок	техническое заключение; фото с рулеткой и привязкой к стене или углу	К-20 Результат принимает: Архитектор
О-10	Спальня 1, ванная, гардеробная, прихожая, кухня-гостиная, санузел 2	Обмер	Углы и диагонали помещений с кухней, санузлами, гардеробной и встроенной мебелью: длины сторон и обе диагонали каждого, отклонения углов от 90° у стен под встроенную мебель и плитку. Прямые углы отмечаются на листах только после этого замера.	Архитектор	±5 мм; диагонали — разница от 5 мм подписывается	Отметки прямых углов 90°; размеры стен под встроенную мебель и плитку. Листы: л. 27 — Обмерный план л. 32 — План расстановки мебели	акт контрольного обмера	К-21 Результат принимает: Архитектор

Допущения и предложения на листе

Основа листа: размеры сняты со скана плана заказчика по размерным цепочкам, контрольный обмер на объекте не выполнялся (К-13); высота потолка 2700 мм принята: на плане заказчика не указана (К-11); толщины стен приняты: наружные 250 мм, перегородки 150 мм (на плане 85–190 мм) (К-13); разрешённая мощность 15 кВт принята по типовой квартире, технических условий нет (К-14); утолщение стены 190 × 1360 мм и элемент 1470 × 160 мм плана заказчика не определены (К-12); ниши санузла 2 закрыты перегородкой и фальш-стеной: проектное решение, на плане заказчика ниша у входа открыта (К-18); несущие стены не определены: до технического заключения все существующие стены считаются несущими (К-20); окна существующие и сохраняются; подоконная доска и глубина откосов не заданы — приняты, не замерены (К-27); подрайон климата не задан — принят не северный (жилые от 2,5 м) (К-29).

Знак «*» — принято, не замерено и не подтверждено (замерить на объекте): К-17: Ст К1-1, Ст В1-1, Ст К1-2, Ст В1-2.

См. лист открытых вопросов (лист 7, записи К-11–К-14, К-17, К-18, К-20; лист 8, записи К-27, К-29).

Изм.	Кол.уч	Лист	№ док.	Подп.	Дата
Разраб.		Кырлан А.С.			13.11.26
Пров.					
ГИП					
Н. контр.					
Утв.					

ГД-2026-003-АИ

Трёхкомнатная квартира

Общая площадь 78,95* м² · * размеры со скана, не замерены (реестр — л. 6–11, К-13)

Дизайн-проект интерьера трёхкомнатной квартиры

Стадия	Лист	Листов
РП	13	132

Задание на контрольный обмер и обследование.
Лист 2 из 5
М б/м

Кырлан Александр Сергеевич

выпуск 13.11.2026 № 6f3a8abb2c · стр. 13 из 157

Задание на контрольный обмер и обследование. Лист 3 из 5

Что замерить, вскрыть и получить до заказа материалов и изделий

Этап 1. До демонтажа (продолжение)

№	Где	Способ	Что сделать	Кто выполняет	Точность	Что пересчитается в альбоме	Чем подтверждается	Закрывает вопросы реестра
О-11	Прихожая (пом. 5), стена В (входная дверь квартиры)	Обследование	Входная дверь Д-1: в какую сторону открывается полотно, где петли (левая или правая), что в проёме (коробка, наличники, откосы), ширина и высота проёма в чистоте.	Архитектор	±5 мм	Дуга открывания и графа «Откр.» ведомости заполнения проёмов; позиция «Входная дверь» в ведомости объёмов работ и смете. Листы: л. 30 — План дверей и ведомость заполнения проёмов	фото с рулеткой и привязкой к стене или углу; акт контрольного обмера	К-26 Результат принимает: Архитектор
О-12	Спальня 1 (пом. 1), спальня 2 (пом. 4), кухня-гостиная (пом. 6): все окна наружной стены	Обмер	Окна ОК-1…ОК-4: ширина и высота проёма, высота низа окна от пола, подоконная доска (есть или нет, вылет), глубина откоса и коробка окна, состояние блока.	Архитектор	±5 мм	Откосы и подоконники в ведомости объёмов работ; размеры и высота низа окон в ведомости заполнения проёмов; шторы и карнизы у окон. Листы: л. 30 — План дверей и ведомость заполнения проёмов	акт контрольного обмера; фото с рулеткой и привязкой к стене или углу	К-27 Результат принимает: Архитектор
О-13	По месту	Обмер	Подтвердить на объекте принятое: окна существующие и сохраняются; подоконная доска и глубина откосов не заданы приняты, не замерены	Архитектор	±5 мм	Листы, где используется принятая величина. Листы: л. 2–5 — Общие данные	акт контрольного обмера	К-27 Результат принимает: Архитектор
О-14	По месту	Обмер	Подтвердить на объекте принятое: подрайон климата не задан — принят не северный (жилые от 2,5 м)	Архитектор	±5 мм	Листы, где используется принятая величина. Листы: л. 2–5 — Общие данные	акт контрольного обмера	К-29 Результат принимает: Архитектор
О-15	Прихожая (пом. 5): дверь пом. 5, стена В	Обмер	Дверь пом. 5, стена В: положение (привязки к ближайшим углам), ширина, высота, толщина стены в проёме. Принято в проекте: входная дверь существующая; по плану заказчика полотно открывается наружу, в общий коридор — направление взято с плана и на объекте не проверено; остаётся ли существующий блок или он заменяется — не решено (К-26).	Архитектор	±5 мм	Проёмы на обмерном плане и в ведомости проёмов; привязки мебели и выводов к проёмам. Листы: л. 27 — Обмерный план л. 30 — План дверей и ведомость заполнения проёмов	акт контрольного обмера; фото с рулеткой и привязкой к стене или углу	К-26 Результат принимает: Архитектор
О-16	Спальня 1 (пом. 1), ванная (пом. 2), гардеробная (пом. 3), спальня 2 (пом. 4), коридор (пом. 8): дверные проёмы Д-2, Д-3, Д-4	Обмер	Проёмы скрытых дверей Д-2 (спальня 1 и спальня 2), Д-3 и Д-4 в чистоте после снятия отделки: ширина и высота проёма, отвес и диагонали проёма, толщина стены в проёме (у Д-3 и Д-4 по скану 85 мм при принятых 150 мм), привязка проёма к углу помещения. Модель и размеры короба и полотна — по документам изготовителя выбранного блока.	Архитектор	±5 мм; толщина стены ±5 мм	Размер проёма и привязки на плане дверей; размер полотна и короба в ведомости заполнения проёмов; узел скрытой двери (толщина стены 85 или 150 мм); заказ скрытых дверей. Листы: л. 30 — План дверей и ведомость заполнения проёмов л. 114 — Узлы. Лист 1 из 2	акт контрольного обмера; фото с рулеткой и привязкой к стене или углу	К-25 Результат принимает: Архитектор

Этап 2. После демонтажа, до черновых работ

№	Где	Способ	Что сделать	Кто выполняет	Точность	Что пересчитается в альбоме	Чем подтверждается	Закрывает вопросы реестра
О-17	Спальня 1 (пом. 1), Ванная (пом. 2), Гардеробная (пом. 3), Спальня 2 (пом. 4), Прихожая (пом. 5), Кухня-гостиная (пом. 6), Санузел 2 (пом. 7), Коридор (пом. 8)	Обмер	Вертикаль и плоскостность стен: отклонение от вертикали по высоте стены (отвес или лазерный уровень), просвет под правилом 2 м, кривизна углов. Нужно там, где от стены зависит изделие: облицовка плиткой (пом. 2, 7), штукатурка и окраска (пом. 1, 2, 3, 4, 5, 6, 7, 8), встроенная мебель и кухня (пом. 1, 5, 6).	Архитектор	до 1 мм на 2 м (правило и клиновой щуп); вертикаль — мм на высоту стены, отклонения подписываются на плане	Толщина штукатурки и расход смеси в ВОР и спецификации; раскладка плитки (подрезка у стен); зазоры и крепление встроенной мебели и кухни. Листы: л. 62–65 — Раскладка плитки л. 67, 68 — Ведомость отделки помещений	акт контрольного обмера	Вопроса в реестре нет: Альбом принимает стены ровными и вертикальными без замера. Результат принимает: Отделочник

Допущения и предложения на листе

Основа листа: размеры сняты со скана плана заказчика по размерным цепочкам, контрольный обмер на объекте не выполнялся (К-13); высота потолка 2700 мм принята: на плане заказчика не указана (К-11); толщины стен приняты: наружные 250 мм, перегородки 150 мм (на плане 85–190 мм) (К-13); разрешённая мощность 15 кВт принята по типовой квартире, технических условий нет (К-14); утолщение стены 190 × 1360 мм и элемент 1470 × 160 мм плана заказчика не определены (К-12); ниши санузла 2 закрыты перегородкой и фальш-стеной: проектное решение, на плане заказчика ниша у входа открыта (К-18); несущие стены не определены: до технического заключения все существующие стены считаются несущими (К-20); окна существующие и сохраняются; подоконная доска и глубина откосов не заданы — приняты, не замерены (К-27); подрайон климата не задан — принят не северный (жилые от 2,5 м) (К-29).

См. лист открытых вопросов (лист 7, записи К-11–К-14, К-18, К-20; лист 8, записи К-27, К-29).

Изм.	Кол.уч	Лист	№ док.	Подп.	Дата
Разраб.		Кырлан А.С.			13.11.26
Пров.					
ГИП					
Н. контр.					
Утв.					

ГД-2026-003-АИ

Трёхкомнатная квартира

Общая площадь 78,95* м² · * размеры со скана, не замерены (реестр — л. 6–11, К-13)

Дизайн-проект интерьера трёхкомнатной квартиры

Стадия	Лист	Листов
РП	14	132

Задание на контрольный обмер и обследование.
Лист 3 из 5
М б/м

Кырлан Александр Сергеевич

Задание на контрольный обмер и обследование. Лист 4 из 5

Что замерить, вскрыть и получить до заказа материалов и изделий

Этап 3. После черновых работ, до чистового пола

№	Где	Способ	Что сделать	Кто выполняет	Точность	Что пересчитается в альбоме	Чем подтверждается	Закрывает вопросы реестра
О-18	Кухня-гостиная (пом. 6), зона кухни	Обмер	Габариты кухни по готовым стенам: размеры после штукатурки и выравнивания, отметки чистых стен под гарнитур.	Архитектор	±5 мм	Размеры гарнитура и привязки выводов техники к чистым стенам. Листы: л. 81 — Кухня (пом. 6). Развёртка гарнитура л. 37 — План розеток и электровыводов	акт контрольного обмера	К-8 Результат принимает: Мебельщик

Документы и данные закупки (не на объекте)

№	У кого, откуда	Способ	Что получить	К какому сроку	Что пересчитается в альбоме	Чем подтверждается	Закрывает вопросы реестра
О-19	Образец и паспорт партии от поставщика плитки	Закупка	Артикул плитки и калибр партии (фактический размер плитки) для ванной и санузла 2.	До заказа плитки и раскладки	Раскладка плитки: пол 600 × 600 мм и стены 600 × 1200 мм приняты по номинальным размерам; подрезка у стен; количество плитки. Листы: л. 62 — Раскладка плитки. Планы полов л. 64 — Раскладка плитки. Ванная. Развёртки стен л. 65 — Раскладка плитки. Санузел 2. Развёртки стен	паспорт изделия или партии; образец	К-2 Результат принимает: Плиточник
О-20	Заказчик; организация, выдавшая технические условия	Документ	Технические условия на присоединение: разрешённая мощность (принято 15 кВт по типовой квартире, расчётная 11,8 кВт).	До утверждения однолинейной схемы щита	Однолинейная схема щита: вводной аппарат и группы; сверка расчётной мощности 11,8 кВт с разрешённой. Листы: л. 42 — Однолинейная схема щита	копия документа	К-14 Результат принимает: Инженер-электрик
О-21	Заказчик (документы на квартиру и дом)	Документ	Проект дома и план БТИ: тип и серия дома, какие стены несущие.	До любого демонтажа, проёмов и штробления в стенах	Разметка несущих и ненесущих стен на обмерном плане и плане демонтажа; допустимость демонтажа, проёмов и штроб (пока все стены считаются несущими). Листы: л. 28 — План демонтажа и монтажа перегородок	копия документа	К-20 Результат принимает: Архитектор
О-22	Образцы и паспорта изделий от поставщика; код изделия производителя	Закупка	Артикулы изделий отделки: инженерная доска 14/4 мм (дуб натуральный, масло, 1-полосная); керамогранит пола ректифицированный под травертин, матовый, 600 × 600 × 9 мм (пом. 2, 7) и 600 × 1200 × 9 мм (пом. 5); керамогранит стен под травертин, матовый, 600 × 1200 × 9 мм (пом. 2, 7); керамогранит фартука кухни 1200 × 600 × 9 мм (пом. 6); плинтус МДФ под покраску 80 × 16 мм.	До заказа материалов	Ведомость отделки помещений, спецификации материалов, количество упаковок и смета: подсчёт по номинальным размерам заменить подсчётом по выбранным изделиям. Листы: л. 62 — Раскладка плитки. Планы полов л. 63 — Раскладка плитки. Прихожая. Фартук кухни л. 64 — Раскладка плитки. Ванная. Развёртки стен л. 65 — Раскладка плитки. Санузел 2. Развёртки стен л. 66 — План полов л. 67 — Ведомость отделки помещений. Лист 1 из 2 л. 70 — Спецификация отделочных материалов л. 88 — Реестр марок отделки и позиций альбома л. 120–122 — Спецификация материалов л. 123, 124 — Смета ориентировочная	паспорт изделия или партии; образец	К-23 Результат принимает: Отделочник
О-23	Поставщик или изготовитель техники; паспорт и монтажная схема выбранной модели	Закупка	Модели и монтажные схемы встраиваемой техники: холодильник (М6**) и посудомоечная машина (М14*) — габариты ниши, вентзазоры, высота цоколя и решётки, подключение; модель вытяжки М15** и её паспорт.	До заказа модулей кухни	Размеры ниш модулей М6** и М14*; вентиляция в цоколе и за корпусом; точки подключения техники на листе кухни. Листы: л. 81 — Кухня (пом. 6). Развёртка гарнитура л. 83 — Кухня (пом. 6). Монтажная схема	паспорт изделия или партии	К-24 Результат принимает: Мебельщик

Допущения и предложения на листе

Основа листа: размеры сняты со скана плана заказчика по размерным цепочкам, контрольный обмер на объекте не выполнялся (К-13); высота потолка 2700 мм принята: на плане заказчика не указана (К-11); толщины стен приняты: наружные 250 мм, перегородки 150 мм (на плане 85–190 мм) (К-13); разрешённая мощность 15 кВт принята по типовой квартире, технических условий нет (К-14); утолщение стены 190 × 1360 мм и элемент 1470 × 160 мм плана заказчика не определены (К-12); ниши санузла 2 закрыты перегородкой и фальш-стеной: проектное решение, на плане заказчика ниша у входа открыта (К-18); несущие стены не определены: до технического заключения все существующие стены считаются несущими (К-20); окна существующие и сохраняются; подоконная доска и глубина откосов не заданы — приняты, не замерены (К-27); подрайон климата не задан — принят не северный (жилые от 2,5 м) (К-29).

Знак «*» — принято, не замерено и не подтверждено (замерить на объекте): К-8: М14.

Знак «**» — предложение проектировщика, заказчиком не утверждено (согласовать с заказчиком): ИЗ-5, К-8: М6, М15.

См. лист открытых вопросов (лист 6, запись К-8; лист 7, записи К-11–К-14, К-18, К-20; лист 8, записи К-27, К-29; лист 9, запись ИЗ-5).

						ГД-2026-003-АИ		
						Трёхкомнатная квартира Общая площадь 78,95* м² · * размеры со скана, не замерены (реестр — л. 6–11, К-13)		
Изм.	Кол.уч	Лист	№ док.	Подп.	Дата	Дизайн-проект интерьера трёхкомнатной квартиры	Стадия: РП	Лист: 15 / Листов: 132
Разраб.		Кырлан А.С.			13.11.26	**Задание на контрольный обмер и обследование.** **Лист 4 из 5** М б/м	**Кырлан Александр Сергеевич**	
Пров.								
ГИП								
Н. контр.								
Утв.								

выпуск 13.11.2026 № 6f3a8abb2c · стр. 15 из 157

Задание на контрольный обмер и обследование. Лист 5 из 5

Что замерить, вскрыть и получить до заказа материалов и изделий

Документы и данные закупки (не на объекте) (продолжение)

№	У кого, откуда	Способ	Что получить	К какому сроку	Что пересчитается в альбоме	Чем подтверждается	Закрывает вопросы реестра
О-24	Поставщики и изготовители выбранных изделий	Закупка	Срок поставки или изготовления каждой позиции с длинной поставкой: скрытые двери (короб и полотно), кухонный гарнитур, встраиваемая техника, керамогранит, инженерная доска, сантехника и инсталляции, встроенная мебель по замеру цеха после выбора модели, в письменном виде.	До назначения даты заказа каждой позиции	График закупок и работ: срок поставки и последний срок заказа по каждой позиции; смета ориентировочная: графа «Срок поставки»; ведомость объёмов работ. Листы: л. 17–20 — График закупок и работ л. 123, 124 — Смета ориентировочная л. 116–119 — Ведомость объёмов работ	копия документа	К-28 Результат принимает: Прораб-координатор
О-25	адрес объекта, СП 131.13330	Документ	Климатический подрайон по СП 131.13330 (по адресу объекта)	до заказа каркаса потолков	план потолков, разрезы, ведомость объёмов Листы: л. 59 — План потолков	копия документа	К-29 Результат принимает: Архитектор
О-26	Поставщик стиральной машины; модель пока не выбрана	Закупка	Паспорт или монтажная схема выбранной модели: П4* — габарит, высота, тип загрузки, положение подводки и слива. Принято в проекте: вертикальная загрузка 400 × 600 мм — условие закупки (решение автора, ИЗ-11); модель не выбрана, габарит сверить по паспорту.	До закрытия люка и разводки	Габариты и положение изделий на планах и развёртках, выводы (вода, слив, электро), монтажные зазоры; знак «*» у марки снимается паспортом или чертежом. Габарит и подводка П4*; зазоры в ванной (К-1). Листы: л. 48 — План выводов сантехники л. 56 — Спецификация сантехнического оборудования	паспорт изделия или партии	К-19 Результат принимает: Инженер ВК (вода, канализация)
О-27	Изготовитель кухонного гарнитура; проект кухни заказчиком не утверждён	Документ	Чертёж или монтажная схема изготовителя: М7* (модуль нижний с мойкой) — габарит мойки, положение смесителя и сифона, высота рабочей поверхности, М14* (модуль под встраиваемую посудомоечную машину) — габарит ниши, положение подводки и слива, мощность, М8* (модуль нижний) — габариты, положение и выводы (вода, слив, электро) по паспорту выбранной модели. Принято в проекте: М7*: габарит 800 × 600 мм — по данным проекта, не по паспорту, М14*: габарит 600 × 600 мм — по данным проекта, не по паспорту, Ряд М6**…М8* стена-в-стену: было 600+800+600+1800 = 3800 от x 9730 до черновой грани стены Б (13530); чистовая длина стены по развёртке 3770 (отделка 15/15) — гарнитур длиннее стены на 30 мм, зазора под компенсатор нет. Стало: М8* 1775 (бутылочница уже на 25), ряд заканчивается на x 13505 — 10 мм зазора до чистовой грани (13515), закрывается планкой-компенсатором. ИЗ-18..	До черновой электрики и сантехники кухни	Габариты и положение изделий на планах и развёртках, выводы (вода, слив, электро), монтажные зазоры; знак «*» у марки снимается паспортом или чертежом. Выводы кухонной техники на планах розеток и выводов; развёртка гарнитура. Листы: л. 81 — Кухня (пом. 6). Развёртка гарнитура л. 37 — План розеток и электровыводов	копия документа	К-8 Результат принимает: Мебельщик
О-28	Поставщик изделий; Кухня-гостиная (пом. 6)	Закупка	Паспорт или монтажная схема выбранной модели: П11* (мойка кухонная врезная) — габарит мойки, положение смесителя и сифона, высота рабочей поверхности, П12* (посудомоечная машина встраиваемая) — габарит ниши, положение подводки и слива, мощность. Принято в проекте: Размер мойки — один источник: вырез в столешнице М7* на плане столешницы и в ведомости техники 700×480, в данных прибора было 500×450. Принято 700×480 (чаша с крылом), x 10380…11080 в модуле М7* (10330…11130)., П12*: габарит 600 × 600 мм — по данным проекта, не по паспорту.	До закрытия трасс и разводки	Габариты и положение изделий на планах и развёртках, выводы (вода, слив, электро), монтажные зазоры; знак «*» у марки снимается паспортом или чертежом. Листы: л. 32 — План расстановки мебели	паспорт изделия или партии	К-8 Результат принимает: Мебельщик

Примечания

1. Подтверждение: акт контрольного обмера (дата, кто присутствовал, прибор, перечень промеров с результатами, подписи присутствующих); к акту — фото вскрытий и узлов и техническое заключение организации, выполнившей обследование.
2. Номера листов — по ведомости рабочих чертежей комплекта (лист «Общие данные»).
3. Пункт исключается из задания при следующем выпуске, когда акт подписан, значение внесено в проект и листы перевыпущены; знак «*» у величины снимается только замером.

Допущения и предложения на листе

Основа листа: размеры сняты со скана плана заказчика по размерным цепочкам, контрольный обмер на объекте не выполнялся (К-13); высота потолка 2700 мм принята: на плане заказчика не указана (К-11); толщины стен приняты: наружные 250 мм, перегородки 150 мм (на плане 85–190 мм) (К-13); разрешённая мощность 15 кВт принята по типовой квартире, технических условий нет (К-14); утолщение стены 190 × 1360 мм и элемент 1470 × 160 мм плана заказчика не определены (К-12); ниши санузла 2 закрыты перегородкой и фальш-стеной: проектное решение, на плане заказчика ниша у входа открыта (К-18); несущие стены не определены: до технического заключения все существующие стены считаются несущими (К-20); окна существующие и сохраняются; подоконная доска и глубина откосов не заданы — приняты, не замерены (К-27); подрайон климата не задан — принят не северный (жилые от 2,5 м) (К-29).

Знак «*» — принято, не замерено и не подтверждено (замерить на объекте): ИЗ-11, К-19: П4 — вертикальная загрузка 400 × 600 мм — условие закупки (решение автора, ИЗ-11); модель не выбрана, габарит сверить по паспорту; К-8: М7, М14, П12; М8 — Ряд М6…М8 стена-в-стену: было 600+800+600+1800 = 3800 от x 9730 до черновой грани стены Б (13530); чистовая длина стены по развёртке 3770 (отделка 15/15) — гарнитур длиннее стены на 30 мм, зазора под компенсатор нет; П11 — Размер мойки — один источник: вырез в столешнице М7 на плане столешницы и в ведомости техники 700×480, в данных прибора было 500×450.

Знак «**» — предложение проектировщика, заказчиком не утверждено (согласовать с заказчиком): ИЗ-5, К-8: М6.

См. лист открытых вопросов (лист 6, запись К-8; лист 7, записи К-11–К-14, К-18–К-20; лист 8, записи К-27, К-29; лист 9, запись ИЗ-5; лист 10, запись ИЗ-11).

Изм.	Кол.уч	Лист	№ док.	Подп.	Дата
Разраб.		Кырлан А.С.			13.11.26
Пров.					
ГИП					
Н. контр.					
Утв.					

ГД-2026-003-АИ

Трёхкомнатная квартира

Общая площадь 78,95* м² · * размеры со скана, не замерены (реестр — л. 6–11, К-13)

Дизайн-проект интерьера трёхкомнатной квартиры

Стадия	Лист	Листов
РП	16	132

Задание на контрольный обмер и обследование.
Лист 5 из 5
М б/м

Кырлан Александр Сергеевич

выпуск 13.11.2026 № 6f3a8abb2c · стр. 16 из 157

График закупок и работ. Лист 1 из 4

ПРЕДВАРИТЕЛЬНО · не для производства работ · открыто пунктов: 28 (реестр — л. 6–11)

Что заказывать и когда не раньше чего: относительный порядок без дат; срок поставки — из данных или «не задан» с записью реестра

Лист не содержит дат: контрольного обмера, подписанных решений автора и договоров ещё нет, и любая дата была бы выдумана. Вместо календаря — порядок и условия: замер → решение и выбор изделия → заказ → срок поставки → работа, которую позиция блокирует.
Срок поставки печатается как срок, только если он задан в данных позиции. Нет — «срок поставки не задан» и ссылка на вопрос реестра о сроках; типовой диапазон практики стоит рядом как ориентир и заказывать по нему нельзя. Номера З-N и Р-N — строки этого листа, К-N — записи реестра открытых вопросов, О-N — позиции задания на контрольный обмер.

Закупки: что заказывается, от чего зависит заказ и какую работу блокирует

№	Позиция и где	1. Замер до заказа	2. Решение, выбор изделия, паспорт	3. Условие заказа	4. Срок поставки	5. Блокирует работу	Закрывает вопросы реестра
З-1	Двери скрытого монтажа с коробом под покраску в новой перегородке П-1**: Д-5 — 1 шт. пом. 6	О-16: обмер: Спальня 1 (пом. 1), ванная (пом. 2), гардеробная (пом. 3), спальня 2 (пом. 4), коридор (пом. 8): дверные проёмы Д-2, Д-3, Д-4 (К-25) О-6: обмер: Вся квартира, все помещения; обход по часовой стрелке от входа (К-13, К-18)	Скрытые двери Д-2 (спальня 1 и спальня 2), Д-3 (ванная) и Д-4 (гардеробная) заданы размером проёма 800×2100 со скана плана заказчика; проёмы существующие, расширять их до технического заключения (К-20) нельзя. (К-25) Санузел 2: ниша 1600 × 1840 мм у входа закрыта перегородкой, ниша 660 × 260 мм (уступ по плану) — фальш-стеной с рамой инсталляции: проектное решение, на плане заказчика ниша у входа открыта в кухню-гостиную. (К-18) Вход в санузел 2 (с унитазом) — из кухни-гостиной: так по плану заказчика (ниша у входа на плане открыта в кухню-гостиную, в проекте закрыта перегородкой по линии низа прихожей). (К-4)	После 1 и 2 и после получения срока у поставщика (К-28); дата заказа — когда срок известен, не позднее чем за срок до начала Р-3.	срок поставки не задан (запись реестра К-28) Ориентир практики (не срок поставщика): ≈ 30 дн.	Р-3 «перегородки ГКЛ»: коробку ставят в каркас перегородки до обшивки (работа по перегородкам); полотно навешивают после чистовой отделки стен	К-4, К-13, К-18, К-25, К-28
З-2	Двери скрытого монтажа с коробом под покраску в существующих проёмах: Д-2, Д-3, Д-4 — 4 шт. пом. 1, 4, 8	О-16: обмер: Спальня 1 (пом. 1), ванная (пом. 2), гардеробная (пом. 3), спальня 2 (пом. 4), коридор (пом. 8): дверные проёмы Д-2, Д-3, Д-4 (К-25) О-6: обмер: Вся квартира, все помещения; обход по часовой стрелке от входа (К-13, К-18)	Скрытые двери Д-2 (спальня 1 и спальня 2), Д-3 (ванная) и Д-4 (гардеробная) заданы размером проёма 800×2100 со скана плана заказчика; проёмы существующие, расширять их до технического заключения (К-20) нельзя. (К-25)	После 1 и 2 и после получения срока у поставщика (К-28); дата заказа — когда срок известен, не позднее чем за срок до начала Р-6.	срок поставки не задан (запись реестра К-28) Ориентир практики (не срок поставщика): ≈ 30 дн.	Р-6 «штукатурка»: короб ставят до штукатурки (коробку ставят на черновой стадии; полотно навешивают после чистовой отделки стен)	К-13, К-18, К-25, К-28
З-3	Кухонный гарнитур по проекту кухни: модули М6**, М7*, М14*, М8*, М13, М15** пом. 6	О-18: обмер: Кухня-гостиная (пом. 6), зона кухни (К-8)	О-27: Чертёж или монтажная схема изготовителя: М7* (модуль нижний с мойкой) — габарит мойки, положение смесителя и сифона, высота рабочей поверхности, М14* (модуль под встраиваемую посудомоечную машину) габарит ниши, положение подводки и слива, мощность, М8* (модуль нижний) габариты, положение и выводы (вода, слив, электро) по паспорту выбранной модели. (К-8); до черновой электрики и сантехники кухни Проект кухни не утверждён заказчиком: выводы кухонной техники (мойка М7*, посудомоечная М14*, варочная панель и духовой шкаф М8*, вытяжка М15**, холодильник М6**) приняты по типовой расстановке техники. (К-8)	После 1 и 2 и после получения срока у поставщика (К-28); дата заказа — когда срок известен, не позднее чем за срок до начала Р-16.	срок поставки не задан (запись реестра К-28) Ориентир практики (не срок поставщика): 4–8 нед. от замера	Р-16 «кухня и мебель»: замер кухни — по готовым стенам после штукатурки или плитки, до чистового пола; производство идёт параллельно со стяжкой и отделкой	К-8, К-28

Допущения и предложения на листе

Основа листа: размеры сняты со скана плана заказчика по размерным цепочкам, контрольный обмер на объекте не выполнялся (К-13); высота потолка 2700 мм принята: на плане заказчика не указана (К-11); толщины стен приняты: наружные 250 мм, перегородки 150 мм (на плане 85–190 мм) (К-13); разрешённая мощность 15 кВт принята по типовой квартире, технических условий нет (К-14); утолщение стены 190 × 1360 мм и элемент 1470 × 160 мм плана заказчика не определены (К-12); ниши санузла 2 закрыты перегородкой и фальш-стеной: проектное решение, на плане заказчика ниша у входа открыта (К-18); несущие стены не определены: до технического заключения все существующие стены считаются несущими (К-20); окна существующие и сохраняются; подоконная доска и глубина откосов не заданы — приняты, не замерены (К-27); подрайон климата не задан — принят не северный (жилые от 2,5 м) (К-29).

Знак «*» — принято, не замерено и не подтверждено (замерить на объекте): К-8: М7, М14; М8 — Ряд М6…М8 стена-в-стену: было 600+800+600+1800 = 3800 от х 9730 до черновой грани стены Б (13530); чистовая длина стены по развёртке 3770 (отделка 15/15) — гарнитур длиннее стены на 30 мм, зазора под компенсатор нет.

Знак «**» — предложение проектировщика, заказчиком не утверждено (согласовать с заказчиком): ИЗ-5, К-8: М6, М15; К-4, К-18: П-1 — проектное решение исполнителя: на плане заказчика ниша у входа открыта в кухню-гостиную; конструкция не утверждена автором (вопрос К-18), положение и размеры сняты со скана (К-13).

Открытые вопросы и конфликты по листу: К-28.

См. лист открытых вопросов (лист 6, записи К-4, К-8; лист 7, записи К-11–К-14, К-18, К-20; лист 8, записи К-27–К-29; лист 9, запись ИЗ-5).

Изм.	Кол.уч	Лист	№ док.	Подп.	Дата
Разраб.		Кырлан А.С.			13.11.26
Пров.					
ГИП					
Н. контр.					
Утв.					

ГД-2026-003-АИ

Трёхкомнатная квартира

Общая площадь 78,95* м² · * размеры со скана, не замерены (реестр — л. 6–11, К-13)

Дизайн-проект интерьера трёхкомнатной квартиры

Стадия	Лист	Листов
РП	17	132

График закупок и работ. Лист 1 из 4

М б/м

Кырлан Александр Сергеевич

выпуск 13.11.2026 № 6f3a8abb2c · стр. 17 из 157

График закупок и работ. Лист 2 из 4

Что заказывать и когда не раньше чего: относительный порядок без дат; срок поставки — из данных или «не задан» с записью реестра

Закупки: что заказывается, от чего зависит заказ и какую работу блокирует (продолжение)

№	Позиция и где	1. Замер до заказа	2. Решение, выбор изделия, паспорт	3. Условие заказа	4. Срок поставки	5. Блокирует работу	Закрывает вопросы реестра
З-4	Встраиваемая техника кухни: М6** холодильник, М14* посудомоечная машина, М15** вытяжка пом. 6		О-23: Модели и монтажные схемы встраиваемой техники: холодильник (М6**) и посудомоечная машина (М14*) — габариты ниши, вентзазоры, высота цоколя и решётки, подключение; модель вытяжки М15** и её паспорт. (К-24); до заказа модулей кухни	После 1 и 2 и после получения срока у поставщика (К-28); дата заказа — когда срок известен, не позднее чем за срок до начала Р-16.	срок поставки не задан (запись реестра К-28)	Р-16 «кухня и мебель»: паспорта и монтажные схемы — до изготовления модулей кухни: нишу и вентзазоры задаёт модель, а не типовая схема 60 см	К-24, К-28
З-5	Стиральная машина: П4* (вертикальная загрузка 400 × 600 мм — условие закупки) пом. 2		О-26: Паспорт или монтажная схема выбранной модели: П4* — габарит, высота, тип загрузки, положение подводки и слива. (К-19); до закрытия люка и разводки	После 1 и 2 и после получения срока у поставщика (К-28); дата заказа — когда срок известен, не позднее чем за срок до начала Р-5.	срок поставки не задан (запись реестра К-28)	Р-5 «черновая сантехника»: габарит и подводка — до закрытия люка и разводки	К-19, К-28
З-6	Сантехнические приборы и инсталляции: П1, П2, П3, П11*, П6, П7, П8 пом. 2, 6, 7	О-8: обмер: Ванная (пом. 2), короб Ш1 248 × 459 мм: Ст К1-1*, Ст В1-1*; квартира, короб Ш2 270 × 1840 мм: Ст К1-2*, Ст В1-2*; наличие стояка ГВС, арматуры и счётчиков — по всей квартире (К-17) О-2: обмер: Спальня 1 (пом. 1), Спальня 2 (пом. 4), Кухня-гостиная (пом. 6); у окон	Санузел 2: ниша 1600 × 1840 мм у входа закрыта перегородкой, ниша 660 × 260 мм (уступ по плану) — фальш-стеной с рамой инсталляции: проектное решение, на плане заказчика ниша у входа открыта в кухню-гостиную. (К-18) Вход в санузел 2 (с унитазом) — из кухни-гостиной: так по плану заказчика (ниша у входа на плане открыта в кухню-гостиную, в проекте закрыта перегородкой по линии низа прихожей). (К-4)	После 1 и 2 и после получения срока у поставщика (К-28); дата заказа — когда срок известен, не позднее чем за срок до начала Р-5.	срок поставки не задан (запись реестра К-28)	Р-5 «черновая сантехника»: инсталляцию ставят до обшивки ГКЛВ и до гидроизоляции стены	К-4, К-17, К-18, К-28
З-7	Керамогранит и плитка: 4 поз. по артикулу и формату, 48,96 м² по раскладке пом. 2, 5, 6, 7	О-17: обмер: Спальня 1 (пом. 1), Ванная (пом. 2), Гардеробная (пом. 3), Спальня 2 (пом. 4), Прихожая (пом. 5), Кухня-гостиная (пом. 6), Санузел 2 (пом. 7), Коридор (пом. 8)	О-19: Артикул плитки и калибр партии (фактический размер плитки) для ванной и санузла 2. (К-2); до заказа плитки и раскладки О-22: Артикулы изделий отделки: инженерная доска 14/4 мм (дуб натуральный, масло, 1-полосная); керамогранит пола ректифицированный под травертин, матовый, 600 × 600 × 9 мм (пом. (К-23); до заказа материалов	После 1 и 2 и после получения срока у поставщика (К-28); дата заказа — когда срок известен, не позднее чем за срок до начала Р-10.	срок поставки не задан (запись реестра К-28)	Р-10 «плитка»: калибр партии измеряют до раскладки, раскладку пересчитывают до заказа	К-2, К-23, К-28
З-8	Покрытие пола (доска) и плинтус: пом. 1, 3, 4, 6, 8 пом. 1, 3, 4, 6, 8		О-22: Артикулы изделий отделки: инженерная доска 14/4 мм (дуб натуральный, масло, 1-полосная); керамогранит пола ректифицированный под травертин, матовый, 600 × 600 × 9 мм (пом. (К-23); до заказа материалов	После 1 и 2 и после получения срока у поставщика (К-28); дата заказа — когда срок известен, не позднее чем за срок до начала Р-13.	срок поставки не задан (запись реестра К-28)	Р-13 «чистовые полы»: артикул и партия — до заказа; доску привозят к чистовым полам	К-23, К-28
З-9	Встроенная мебель по замеру цеха: С5, М16 пом. 1, 5	О-6: обмер: Вся квартира, все помещения; обход по часовой стрелке от входа (К-13, К-18)		После 1 и 2 и после получения срока у поставщика (К-28); дата заказа — когда срок известен, не позднее чем за срок до начала Р-16.	срок поставки не задан (запись реестра К-28) Ориентир практики (не срок поставщика): 4–8 нед. от замера	Р-16 «кухня и мебель»: цех замеряет по готовым стенам; производство 4–8 недель идёт параллельно с отделкой	К-13, К-18, К-28

Допущения и предложения на листе

Основа листа: размеры сняты со скана плана заказчика по размерным цепочкам, контрольный обмер на объекте не выполнялся (К-13); высота потолка 2700 мм принята: на плане заказчика не указана (К-11); толщины стен приняты: наружные 250 мм, перегородки 150 мм (на плане 85–190 мм) (К-13); разрешённая мощность 15 кВт принята по типовой квартире, технических условий нет (К-14); утолщение стены 190 × 1360 мм и элемент 1470 × 160 мм плана заказчика не определены (К-12); ниши санузла 2 закрыты перегородкой и фальш-стеной: проектное решение, на плане заказчика ниша у входа открыта (К-18); несущие стены не определены: до технического заключения все существующие стены считаются несущими (К-20); окна существующие и сохраняются; подоконная доска и глубина откосов не заданы — приняты, не замерены (К-27); подрайон климата не задан — принят не северный (жилые от 2,5 м) (К-29).

Знак «*» — принято, не замерено и не подтверждено (замерить на объекте): ИЗ-11, К-19: П4 — вертикальная загрузка 400 × 600 мм — условие закупки (решение автора, ИЗ-11); модель не выбрана, габарит сверить по паспорту; К-8: М14; П11 — Размер мойки — один источник: вырез в столешнице М7 на плане столешницы и в ведомости техники 700×480, в данных прибора было 500×450; К-17: Ст К1-1, Ст В1-1, Ст К1-2, Ст В1-2.

Знак «**» — предложение проектировщика, заказчиком не утверждено (согласовать с заказчиком): ИЗ-5, К-8: М6, М15.

Открытые вопросы и конфликты по листу: К-28.

См. лист открытых вопросов (лист 6, запись К-8; лист 7, записи К-11–К-14, К-17–К-20; лист 8, записи К-27–К-29; лист 9, запись ИЗ-5; лист 10, запись ИЗ-11).

Изм.	Кол.уч	Лист	№ док.	Подп.	Дата
Разраб.		Кырлан А.С.			13.11.26
Пров.					
ГИП					
Н. контр.					
Утв.					

ГД-2026-003-АИ

Трёхкомнатная квартира

Общая площадь 78,95* м² · * размеры со скана, не замерены (реестр — л. 6–11, К-13)

Дизайн-проект интерьера трёхкомнатной квартиры

Стадия	Лист	Листов
РП	18	132

График закупок и работ. Лист 2 из 4

М б/м

Кырлан Александр Сергеевич

выпуск 13.11.2026 № 6f3a8abb2c · стр. 18 из 157

График закупок и работ. Лист 3 из 4

ПРЕДВАРИТЕЛЬНО · не для производства работ · открыто пунктов: 28 (реестр — л. 6–11)

Что заказывать и когда не раньше чего: относительный порядок без дат; срок поставки — из данных или «не задан» с записью реестра

Работы: порядок и что не даёт начать

№	Работа (стадия технологической последовательности)	После	Что должно быть к началу: условия и закупки	Не начинать, пока открыто в реестре
Р-1	Демонтаж покрытий, отделки стен и потолков, дверных блоков и приборов; конструкции, стены и перегородки не трогать до технического заключения (стадия 1)		до начала: запрошены документы на дом и БТИ; контрольный обмер до демонтажа (что видно) сделан	К-20: Несущие стены не определены: проект дома и план БТИ в материалах объекта отсутствуют, тип и серия дома неизвестны, техническое заключение о несущих конструкциях не выполнялось.
Р-2	Контрольный обмер на голых стенах и обследование (задание — лист «Задание на контрольный обмер») (стадия 2)	Р-1	после снятия отделки: видны стояки, каналы, щиток, толщины стен; до заказа всего, что делают по размеру	К-12: Две конструкции плана заказчика не определены: утолщение стены 190 × 1360 мм в гардеробной у спальни 2 (вентблок или пилон) и элемент 1470 × 160 мм на линии простенка кухни-гостиной (пилон, балка или барная стойка).
Р-3	Перегородки и фальш-стены ГКЛ: разметка, каркас, обшивка (стадия 3)	Р-2	до начала: решение по нише санузла 2 принято автором; разметка по плану монтажа подписана; коробка скрытой двери — в каркас до обшивки Закупки к началу: З-1 (двери скрытого монтажа)	К-4: Вход в санузел 2 (с унитазом) — из кухни-гостиной: так по плану заказчика (ниша у входа на плане открыта в кухню-гостиную, в проекте закрыта перегородкой по линии низа прихожей). К-13: Размеры сняты со скана плана заказчика по размерным цепочкам, контрольный обмер на объекте не выполнялся; толщины стен приняты 250 мм (наружные) и 150 мм (перегородки), на плане 85–190 мм. К-18: Санузел 2: ниша 1600 × 1840 мм у входа закрыта перегородкой, ниша 660 × 260 мм (уступ по плану) — фальш-стеной с рамой инсталляции: проектное решение, на плане заказчика ниша у входа открыта в кухню-гостиную. К-20: Несущие стены не определены: проект дома и план БТИ в материалах объекта отсутствуют, тип и серия дома неизвестны, техническое заключение о несущих конструкциях не выполнялось. К-25: Скрытые двери Д-2 (спальня 1 и спальня 2), Д-3 (ванная) и Д-4 (гардеробная) заданы размером проёма 800×2100 со скана плана заказчика; проёмы существующие, расширять их до технического заключения (К-20) нельзя.
Р-4	Черновая электрика: штробы, короба, гофра, подрозетники, щит (стадия 4)	Р-2, Р-3	до начала: план электрики с высотами утверждён; штробы в стенах — только после технического заключения; мебель расставлена	К-14: Разрешённая мощность 15 кВт принята по типовой квартире, технических условий в материалах объекта нет; расчётная мощность 11,8 кВт. К-20: Несущие стены не определены: проект дома и план БТИ в материалах объекта отсутствуют, тип и серия дома неизвестны, техническое заключение о несущих конструкциях не выполнялось.
Р-5	Черновая сантехника и вентиляция: разводка, выводы, инсталляции, короба стояков (стадия 5)	Р-2, Р-3	до начала: положение стояков замерено; модели инсталляций и машины выбраны (габариты рамы, подводка); инсталляцию ставят до обшивки ГКЛВ и до гидроизоляции Закупки к началу: З-5 (стиральная машина), З-6 (сантехника)	К-4: Вход в санузел 2 (с унитазом) — из кухни-гостиной: так по плану заказчика (ниша у входа на плане открыта в кухню-гостиную, в проекте закрыта перегородкой по линии низа прихожей). К-17: Положение стояков условно, на объекте не замерено: стояки канализации и холодной воды — в коробе Ш1 248 × 459 в углу ванной и в стене-пилоне Ш2 270 мм между санузлом 2 и кухней (по плану заказчика). К-18: Санузел 2: ниша 1600 × 1840 мм у входа закрыта перегородкой, ниша 660 × 260 мм (уступ по плану) — фальш-стеной с рамой инсталляции: проектное решение, на плане заказчика ниша у входа открыта в кухню-гостиную. К-19: Модель стиральной машины П4* не выбрана.
Р-6	Коробки скрытых дверей, затем штукатурка стен и откосов (стадия 6)	Р-3, Р-4, Р-5	до начала: электрика и сантехника смонтированы, штробы заделаны; коробки скрытых дверей установлены до штукатурки (поэтому заказ дверей — раньше работы) Закупки к началу: З-2 (двери скрытого монтажа)	К-13: Размеры сняты со скана плана заказчика по размерным цепочкам, контрольный обмер на объекте не выполнялся; толщины стен приняты 250 мм (наружные) и 150 мм (перегородки), на плане 85–190 мм. К-18: Санузел 2: ниша 1600 × 1840 мм у входа закрыта перегородкой, ниша 660 × 260 мм (уступ по плану) — фальш-стеной с рамой инсталляции: проектное решение, на плане заказчика ниша у входа открыта в кухню-гостиную. К-25: Скрытые двери Д-2 (спальня 1 и спальня 2), Д-3 (ванная) и Д-4 (гардеробная) заданы размером проёма 800×2100 со скана плана заказчика; проёмы существующие, расширять их до технического заключения (К-20) нельзя.
Р-7	Стяжка пола и тёплый пол (стадия 7)	Р-6	до начала: штукатурка сделана; трубы под стяжкой приняты; нивелировка плиты выполнена	

Допущения и предложения на листе

Основа листа: размеры сняты со скана плана заказчика по размерным цепочкам, контрольный обмер на объекте не выполнялся (К-13); высота потолка 2700 мм принята: на плане заказчика не указана (К-11); толщины стен приняты: наружные 250 мм, перегородки 150 мм (на плане 85–190 мм) (К-13); разрешённая мощность 15 кВт принята по типовой квартире, технических условий нет (К-14); утолщение стены 190 × 1360 мм и элемент 1470 × 160 мм плана заказчика не определены (К-12); ниши санузла 2 закрыты перегородкой и фальш-стеной: проектное решение, на плане заказчика ниша у входа открыта (К-18); несущие стены не определены: до технического заключения все существующие стены считаются несущими (К-20); окна существующие и сохраняются; подоконная доска и глубина откосов не заданы — приняты, не замерены (К-27); подрайон климата не задан — принят не северный (жилые от 2,5 м) (К-29).

Знак «*» — принято, не замерено и не подтверждено (замерить на объекте): ИЗ-11, К-19: П4 — вертикальная загрузка 400 × 600 мм — условие закупки (решение автора, ИЗ-11); модель не выбрана, габарит сверить по паспорту.

Открытые вопросы и конфликты по листу: К-28.

См. лист открытых вопросов (лист 7, записи К-11–К-14, К-18–К-20; лист 8, записи К-27–К-29; лист 10, запись ИЗ-11).

Изм.	Кол.уч	Лист	№ док.	Подп.	Дата
Разраб.		Кырлан А.С.			13.11.26
Пров.					
ГИП					
Н. контр.					
Утв.					

ГД-2026-003-АИ

Трёхкомнатная квартира

Общая площадь 78,95* м² · * размеры со скана, не замерены (реестр — л. 6–11, К-13)

Дизайн-проект интерьера трёхкомнатной квартиры

Стадия	Лист	Листов
РП	19	132

График закупок и работ. Лист 3 из 4

М б/м

Кырлан Александр Сергеевич

выпуск 13.11.2026 № 6f3a8abb2c · стр. 19 из 157

График закупок и работ. Лист 4 из 4

Что заказывать и когда не раньше чего: относительный порядок без дат; срок поставки — из данных или «не задан» с записью реестра

Работы: порядок и что не даёт начать (продолжение)

№	Работа (стадия технологической последовательности)	После	Что должно быть к началу: условия и закупки	Не начинать, пока открыто в реестре
Р-8	Гидроизоляция санузлов и тест проливом (стадия 8)	Р-7	до начала: стяжка набрала прочность и сухая по инструкции гидроизоляции; выводы стоят на проектных отметках	
Р-9	ГКЛ: короба инсталляции и стояков, ниши, потолки (стадия 9)	Р-4, Р-5	до начала: черновые сети в зоне коробов приняты; закладные под тяжёлое и карнизы стоят; светильники выбраны (вырезы)	
Р-10	Плитка и керамогранит: стены, затем пол; фартук (стадия 10)	Р-7, Р-8, Р-9	до начала: гидроизоляция принята; плитка выбрана, калибр партии измерен, раскладка пересчитана и подписана Закупки к началу: З-7 (плитка)	К-2: Артикул плитки и калибр партии (фактический размер плитки) для ванной и санузла 2 не заданы: раскладка рассчитана по номинальным размерам — пол 600 × 600 мм, стены 600 × 1200 мм. К-23: Артикулы изделий отделки не выбраны.
Р-11	Шпаклёвка стен и потолков под окраску (стадия 11)	Р-6, Р-9, Р-10	до начала: плитка готова (грязные работы закончены); штукатурка и ГКЛ сухие	
Р-12	Окраска стен, потолков, откосов (стадия 13)	Р-11	до начала: шпаклёвка отшлифована и огрунтована; выкрасы утверждены, колеровка одной партией	
Р-13	Чистовые полы: инженерная доска (стадия 14)	Р-10, Р-12	до начала: влажность основания в норме, мокрые работы закончены; доска выбрана и привезена Закупки к началу: З-8 (доска и плинтус)	К-23: Артикулы изделий отделки не выбраны.
Р-14	Полотна межкомнатных дверей, плинтусы, пороги (стадия 15)	Р-12, Р-13	до начала: чистовой пол уложен; полотна скрытых дверей — после чистовой отделки стен	
Р-15	Чистовая электрика и сантехника: механизмы, светильники, смесители, приборы (стадия 16)	Р-12, Р-14	до начала: отделка готова; механизмы, светильники и приборы выбраны и привезены	
Р-16	Кухня, встроенная и корпусная мебель, бытовая техника (стадия 17)	Р-14, Р-15	до начала: чистовая сантехника и электрика подведены к местам мебели; замер кухни снят по готовым стенам (после штукатурки или плитки, до чистового пола) Закупки к началу: З-3 (кухонный гарнитур), З-4 (техника кухни), З-9 (мебель по замеру)	К-8: Проект кухни не утверждён заказчиком: выводы кухонной техники (мойка М7*, посудомоечная М14*, варочная панель и духовой шкаф М8*, вытяжка М15**, холодильник М6**) приняты по типовой расстановке техники. К-13: Размеры сняты со скана плана заказчика по размерным цепочкам, контрольный обмер на объекте не выполнялся; толщины стен приняты 250 мм (наружные) и 150 мм (перегородки), на плане 85–190 мм. К-18: Санузел 2: ниша 1600 × 1840 мм у входа закрыта перегородкой, ниша 660 × 260 мм (уступ по плану) — фальш-стеной с рамой инсталляции: проектное решение, на плане заказчика ниша у входа открыта в кухню-гостиную. К-24: Модели встраиваемой техники кухни не выбраны: холодильник (М6**) и посудомоечная машина (М14*) заданы описанием «аналог по характеристикам» — без производителя, серии и кода.
Р-17	Сдача: осмотр по чек-листу, дефектная ведомость, устранение замечаний (стадия 18)	Р-15, Р-16	до начала: всё смонтировано; акты скрытых работ подписаны	

Примечания

1. Порядок работ — стадии технологической последовательности из 17 позиций, присутствующих в этом проекте (по строкам ведомости объёмов); остальные стадии таблицы knowledge/remont-tehnologiya.md в проекте не встречаются. Длительности работ не печатаются: их нет ни в данных, ни в нормах для этого объекта.
2. Типовые сроки — ориентир практики, не срок поставщика: скрытые двери — короб около 10 дн., полотно под покраску до 3 нед., шпон 4–5 нед., в среднем около 30 дн. (knowledge/workers/foreman.md, п. 2.4 (profil-doors)); кухня и корпусная мебель — 4–8 недель от замера (knowledge/remont-tehnologiya.md, разд. 2; knowledge/workers/foreman.md, п. 2.4). Заказ по ориентиру не назначается: срок получают у поставщика (вопрос реестра), после чего заказ планируют «не позднее чем за срок до начала работы».
3. Условия заказа берутся из реестра открытых вопросов и задания на контрольный обмер: позиция заказывается, когда закрыты замер (графа 1) и решение (графа 2). Закрывать их может только факт или решение автора с подписью; снять строку с листа можно только закрыв запись реестра.
4. Заказ по размеру до контрольного обмера не делают: двери, кухня и встроенная мебель зависят от обмера (К-11, К-13); скрытые двери, кроме того, зависят от решения по нише санузла 2 (проём Д-5 в перегородке П-1**).
5. Номера листов — по ведомости рабочих чертежей комплекта (лист «Общие данные»).

Допущения и предложения на листе

Основа листа: размеры сняты со скана плана заказчика по размерным цепочкам, контрольный обмер на объекте не выполнялся (К-13); высота потолка 2700 мм принята: на плане заказчика не указана (К-11); толщины стен приняты: наружные 250 мм, перегородки 150 мм (на плане 85–190 мм) (К-13); разрешённая мощность 15 кВт принята по типовой квартире, технических условий нет (К-14); утолщение стены 190 × 1360 мм и элемент 1470 × 160 мм плана заказчика не определены (К-12); ниши санузла 2 закрыты перегородкой и фальш-стеной: проектное решение, на плане заказчика ниша у входа открыта (К-18); несущие стены не определены: до технического заключения все существующие стены считаются несущими (К-20); окна существующие и сохраняются; подоконная доска и глубина откосов не заданы — приняты, не замерены (К-27); подрайон климата не задан — принят не северный (жилые от 2,5 м) (К-29).

Знак «*» — принято, не замерено и не подтверждено (замерить на объекте): К-8: М7, М14; М8 — Ряд М6…М8 стена-в-стену: было 600+800+600+1800 = 3800 от х 9730 до черновой грани стены Б (13530); чистовая длина стены по развёртке 3770 (отделка 15/15) — гарнитур длиннее стены на 30 мм, зазора под компенсатор нет.

Знак «**» — предложение проектировщика, заказчиком не утверждено (согласовать с заказчиком): ИЗ-5, К-8: М6, М15; К-4, К-18: П-1 — проектное решение исполнителя: на плане заказчика ниша у входа открыта в кухню-гостиную; конструкция не утверждена автором (вопрос К-18), положение и размеры сняты со скана (К-13).

Открытые вопросы и конфликты по листу: К-28.

См. лист открытых вопросов (лист 6, записи К-4, К-8; лист 7, записи К-11–К-14, К-18, К-20; лист 8, записи К-27–К-29; лист 9, запись ИЗ-5).

Изм.	Кол.уч	Лист	№ док.	Подп.	Дата
Разраб.		Кырлан А.С.			13.11.26
Пров.					
ГИП					
Н. контр.					
Утв.					

ГД-2026-003-АИ

Трёхкомнатная квартира

Общая площадь 78,95* м² · * размеры со скана, не замерены (реестр — л. 6–11, К-13)

Дизайн-проект интерьера трёхкомнатной квартиры

Стадия	Лист	Листов
РП	20	132

График закупок и работ. Лист 4 из 4

М б/м

Кырлан Александр Сергеевич


выпуск 13.11.2026 № 6f3a8abb2c · стр. 20 из 157

Календарный график работ и закупок

ПРЕДВАРИТЕЛЬНО · не для производства работ · открыто пунктов: 28 (реестр — л. 6–11)

Недели, зависимости, техпаузы и даты заказа длинных позиций · длительности — ориентир по таблице типовых сроков, не обещание бригады

№	Работа	Нед.	После
Р-1	**демонтаж**	1,25	
Р-2	**контрольный обмер**	0,5	Р-1
Р-3	**перегородки ГКЛ**	1	Р-2
Р-4	**черновая электрика**	1,75	Р-3, Р-2
Р-5	черновая сантехника	1,25	Р-3, Р-2
Р-6	**штукатурка**	2,5	Р-4, Р-5, Р-3
Р-7	**стяжка**	1	Р-6
Р-8	**гидроизоляция**	0,5	Р-7
Р-9	ГКЛ	1,75	Р-4, Р-5
Р-10	**плитка**	3,5	Р-8, Р-9, Р-7
Р-11	**шпаклёвка**	3	Р-10, Р-9, Р-6
Р-12	**окраска**	2,25	Р-11
Р-13	**чистовые полы**	1,25	Р-12, Р-10
Р-14	**двери и плинтусы**	1	Р-13, Р-12
Р-15	**чистовая электрика и сантехника**	1	Р-14, Р-12
Р-16	**кухня и мебель**	1	Р-15, Р-14
Р-17	**сдача**	0,75	Р-16, Р-15
Закупки: заказать не позднее — «◆»; от заказа до поставки — штриховая полоса; срок поставки — только из данных или «ориентир практики»			
З-1	Двери скрытого монтажа с коробом под покраску в новой перегородке П-1**: Д-5 — 1 шт.	4,25	для Р-3
З-2	Двери скрытого монтажа с коробом под покраску в существующих проёмах: Д-2, Д-3, Д-4 — 4 шт	4,25	для Р-6
З-3	Кухонный гарнитур по проекту кухни: модули М6**, М7*, М14*, М8*, М13, М15**	6	для Р-16
З-4	Встраиваемая техника кухни: М6** холодильник, М14* посудомоечная машина, М15** вытяжка		для Р-16
З-5	Стиральная машина: П4* (вертикальная загрузка 400 × 600 мм — условие закупки)		для Р-5
З-6	Сантехнические приборы и инсталляции: П1, П2, П3, П11*, П6, П7, П8		для Р-5
З-7	Керамогранит и плитка: 4 поз. по артикулу и формату, 48,96 м² по раскладке		для Р-10
З-8	Покрытие пола (доска) и плинтус: пом. 1, 3, 4, 6, 8		для Р-13
З-9	Встроенная мебель по замеру цеха: С5, М16	6	для Р-16

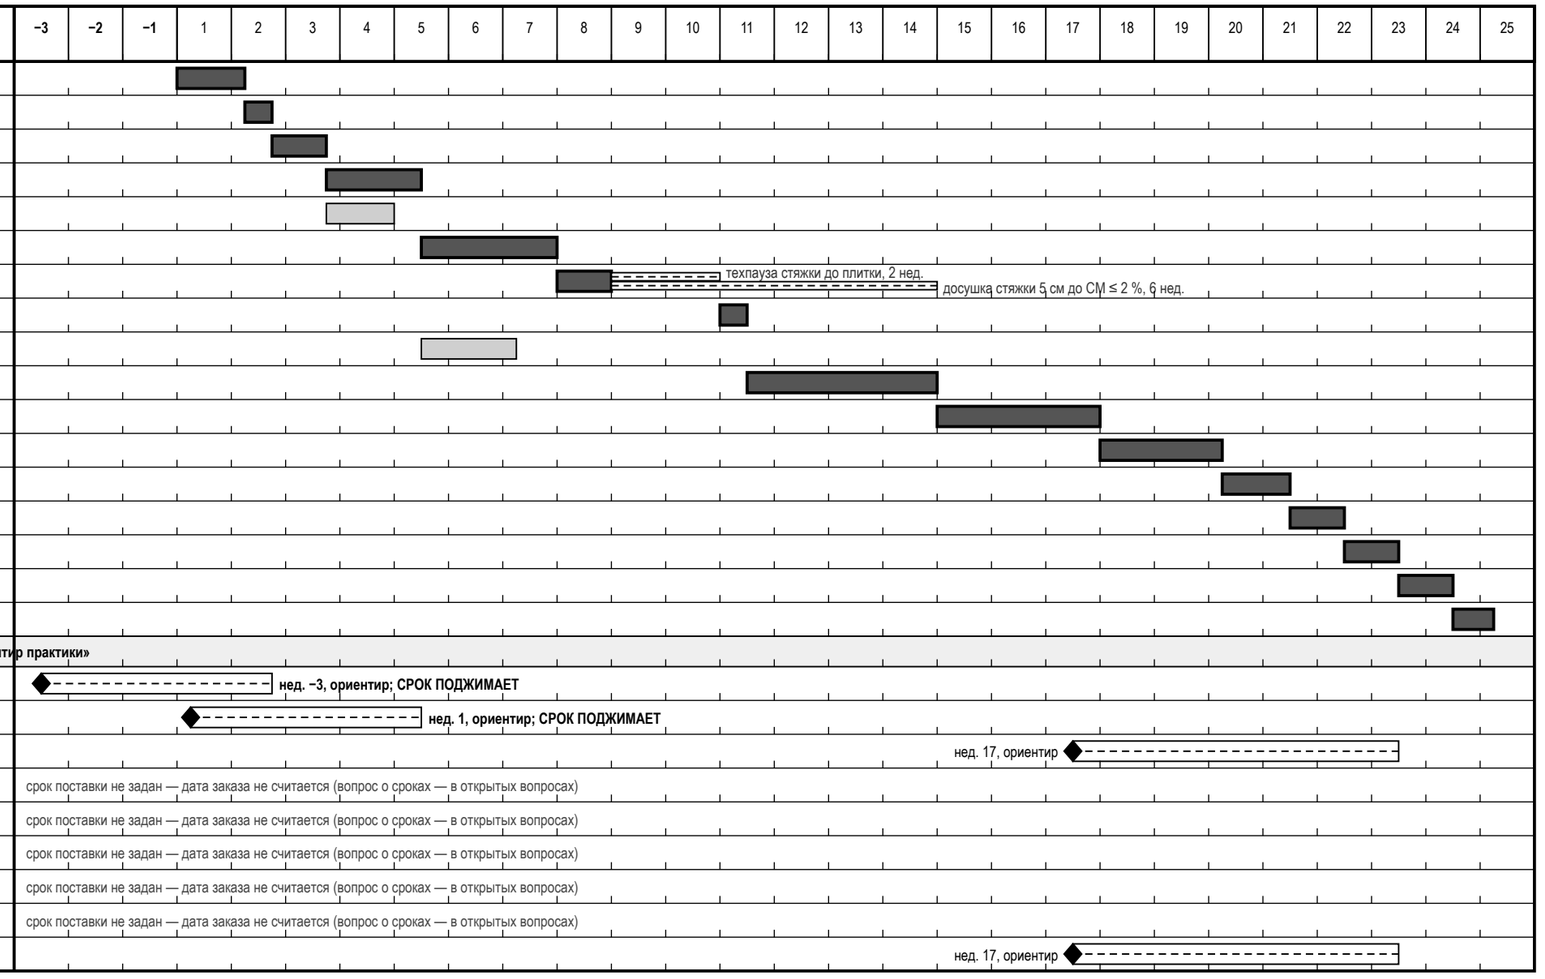

Итого: ≈ 24,25 нед. · жирная линия и тёмная полоса — критический путь

Примечания

1. Длительности этапов — типовые сроки по площади 78,95 м² (таблица «Свод для графика»: недели по этапам для 45, 80 и 120 м², середина вилки, линейная интерполяция); это ориентир, а не норма и не обещание бригады. Контрольный обмер — ориентир 0,5 нед. (в таблице нет).
2. Зависимости «после» — из графика закупок и работ (лист «График закупок и работ»); каждая работа начинается после конца предшественников. Техпаузы стоят отдельными полосами, а не спрятаны в длительности: стяжка → плитка — не менее 2 нед.; стяжка → чистовой пол — досушка стяжки 5 см до СМ ≤ 2 % — 6 нед. (ориентир «1 нед. на 1 см до 4 см, 5 см — 6 нед., 6 см — 8 нед.»; решает замер).
3. График последовательный и поэтому консервативный: в жизни шпаклёвка, плитка и досушка стяжки идут частично параллельно (таблица типовых сроков для 78,95 м²: 16–20 нед.). Совмещения — решение прораба после обмера.
4. Закупки: «заказать не позднее» = начало работы, которой нужна позиция, минус срок поставки. Срок поставки — из данных проекта (срок поставки позиции, срок изготовления обоев в отделке); если его нет, в графике стоит типовой диапазон практики с пометкой «ориентир» — это не срок поставщика, его надо получить до заказа. Кухню и встроенную мебель заказывают после замера по готовым стенам (после штукатурки). Позиции без срока дат заказа не имеют.
5. «Срок поджимает»: самая поздняя дата заказа раньше, чем позицию можно заказать (до замера или обмера): сдвиньте начало работ, ищите изделие с меньшим сроком или заказывайте по предварительному размеру — решение прораба и заказчика.

Допущения и предложения на листе

Основа листа: размеры сняты со скана плана заказчика по размерным цепочкам, контрольный обмер на объекте не выполнялся (К-13); высота потолка 2700 мм принята: на плане заказчика не указана (К-11); толщины стен приняты: наружные 250 мм, перегородки 150 мм (на плане 85–190 мм) (К-13); разрешённая мощность 15 кВт принята по типовой квартире, технических условий нет (К-14); утолщение стены 190 × 1360 мм и элемент 1470 × 160 мм плана заказчика не определены (К-12); ниши санузла 2 закрыты перегородкой и фальш-стеной: проектное решение, на плане заказчика ниша у входа открыта (К-18); несущие стены не определены: до технического заключения все существующие стены считаются несущими (К-20); окна существующие и сохраняются; подоконная доска и глубина откосов не заданы — приняты, не замерены (К-27); подрайон климата не задан — принят не северный (жилые от 2,5 м) (К-29).

Знак «*» — принято, не замерено и не подтверждено (замерить на объекте): ИЗ-11, К-19: П4 — вертикальная загрузка 400 × 600 мм — условие закупки (решение автора, ИЗ-11); модель не выбрана, габарит сверить по паспорту; К-8: М7, М14; М8 — Ряд М6…М8 стена-в-стену: было 600+800+600+1800 = 3800 от х 9730 до черновой грани стены Б (13530); чистовая длина стены по развёртке 3770 (отделка 15/15) — гарнитур длиннее стены на 30 мм, зазора под компенсатор нет; П11 — Размер мойки — один источник: вырез в столешнице М7 на плане столешницы и в ведомости техники 700×480, в данных прибора было 500×450.

Знак «**» — предложение проектировщика, заказчиком не утверждено (согласовать с заказчиком): ИЗ-5, К-8: М6, М15; К-4, К-18: П-1 — проектное решение исполнителя: на плане заказчика ниша у входа открыта в кухню-гостиную; конструкция не утверждена автором (вопрос К-18), положение и размеры сняты со скана (К-13).

См. лист открытых вопросов (лист 6, записи К-4, К-8; лист 7, записи К-11–К-14, К-18–К-20; лист 8, записи К-27, К-29; лист 9, запись ИЗ-5; лист 10, запись ИЗ-11).

Изм.	Кол.уч	Лист	№ док.	Подп.	Дата
Разраб.		Кырлан А.С.			13.11.26
Пров.					
ГИП					
Н. контр.					
Утв.					

ГД-2026-003-АИ

Трёхкомнатная квартира

Общая площадь 78,95* м² · * размеры со скана, не замерены (реестр — л. 6–11, К-13)

Дизайн-проект интерьера трёхкомнатной квартиры

Стадия	Лист	Листов
РП	21	132

Календарный график работ и закупок

М б/м

Кырлан Александр Сергеевич

выпуск 13.11.2026 № 6f3a8abb2c · стр. 21 из 157

Чек-лист приёмки по этапам. Лист 1 из 4

По этапам Р-1…Р-N: что проверить, чем, какой допуск и какой акт подписать до закрытия работы

Приёмка по этапам: контрольные точки, допуски и акты скрытых работ

Этап	Контрольная точка (дальше не пускают без подписи)	Что проверяют	Чем	Допуск	Основание	Подпись	Акт скрытых работ / документ
Р-1	Демонтаж До начала демонтажа: запрошены документы на дом и БТИ	Что снимается и что не трогается: покрытия, отделка, дверные блоки; несущие стены и перегородки — без изменений	осмотр по плану демонтажа	снятое — только по плану; несущее не затрагивать	практика		Фото помещений до и после демонтажа; перечень снятого в журнале работ.
Р-2	Контрольный обмер Контрольный обмер на голых стенах сделан до заказа всего, что делают по размеру	Размеры помещений и проёмов, диагонали, положение стояков, щитка, каналов, толщины стен	рулетка, лазерный дальномер, уровень	допуск задаёт проект; расхождение с планом — в перечень открытых вопросов до заказа	практика		Протокол контрольного обмера с эскизом; расхождения занесены в открытые вопросы.
Р-3	Перегородки ГКЛ Перегородки: разметка против плана монтажа подписана до обшивки	Шаг саморезов: потолок 150 мм; стена 200 мм (лист вертикально) или 300 мм (горизонтально)	рулетка	150 / 200 / 300 мм	практика (СП 163.1325800.2014)		Акт скрытых работ: каркас ГКЛ, закладные под тяжёлое, звукоизоляция в перегородках — до обшивки (фото закладных с привязками); армирование и примыкание к несущим.
		Отступ самореза от кромки и угла листа; расстояние между саморезами на стыке листов	рулетка	5–10 мм от кромки; не менее 15 мм на стыке	практика (СП 163.1325800.2014)		
		Заделка стыков: лента и не менее 2 слоёв шпаклёвки; шляпки утоплены вровень, без прорыва картона	визуально, на просвет	без трещин после высыхания	практика		
		Прогиб каркаса: нет люфта между листом и профилем	простукивание, нажатие рукой	точной цифры нет — сверить перед актом	практика		
Р-4	Черновая электрика Черновая электрика: трассы, высоты подрозетников, замер изоляции подписаны до заделки	Сопротивление изоляции проводки (цепи до 1000 В)	мегаомметр	не менее 0,5 МОм	норматив (ПУЭ, гл. 1.8)		Акт скрытых работ на трассы проводки и слаботочные линии до закрытия штукатуркой и ГКЛ; исполнительная схема трасс с привязками; заземление и уравнивание потенциалов в санузле протокол и фото.
		Целостность и маркировка: PE жёлто-зелёный, N — синий, L — прочие цвета	визуально, прозвонка	каждый проводник промаркирован	практика		
		Высоты подрозетников и привязки — по плану розеток и выключателей	рулетка, уровень	по проекту; от чистого пола	практика		
Р-5	Черновая сантехника Черновая сантехника: опрессовка, отметки выводов, инсталляции подписаны до зашивки	Опрессовка водоснабжения: рабочее давление до 0,6 МПа — испытание 0,9 МПа; выше 0,6 МПа — по расчёту	опрессовочный насос, манометр	выдержка 10 мин (поквартирная); падение: пластик не более 0,06 МПа за 30 мин, сталь не более 0,05 МПа за 10 мин	практика (СП 73.13330)		Акт опрессовки (давление, время, результат); акт скрытых работ на трассы в стенах, полу и коробах; инсталляции, скрытые смесители, трапы — фото с рулеткой и отметками.
		Уклон канализации Ø40–50	уровень, построитель плоскостей	не менее 20 мм на 1 м	норматив (СП 30.13330)		
		Протечки в соединениях, сифоны, смесители, гибкая подводка	осмотр под давлением, салфетка на стыках	нет капель и влажных следов в контрольное время	практика		

Допущения и предложения на листе

Основа листа: размеры сняты со скана плана заказчика по размерным цепочкам, контрольный обмер на объекте не выполнялся (К-13); высота потолка 2700 мм принята: на плане заказчика не указана (К-11); толщины стен приняты: наружные 250 мм, перегородки 150 мм (на плане 85–190 мм) (К-13); разрешённая мощность 15 кВт принята по типовой квартире, технических условий нет (К-14); утолщение стены 190 × 1360 мм и элемент 1470 × 160 мм плана заказчика не определены (К-12); ниши санузла 2 закрыты перегородкой и фальш-стеной: проектное решение, на плане заказчика ниша у входа открыта (К-18); несущие стены не определены: до технического заключения все существующие стены считаются несущими (К-20); окна существующие и сохраняются; подоконная доска и глубина откосов не заданы — приняты, не замерены (К-27); подрайон климата не задан — принят не северный (жилые от 2,5 м) (К-29).

См. лист открытых вопросов (лист 7, записи К-11–К-14, К-18, К-20; лист 8, записи К-27, К-29).

Изм.	Кол.уч	Лист	№ док.	Подп.	Дата
Разраб.		Кырлан А.С.			13.11.26
Пров.					
ГИП					
Н. контр.					
Утв.					

ГД-2026-003-АИ

Трёхкомнатная квартира

Общая площадь 78,95* м² · * размеры со скана, не замерены (реестр — л. 6–11, К-13)

Дизайн-проект интерьера трёхкомнатной квартиры

Стадия	Лист	Листов
РП	22	132

Чек-лист приёмки по этапам. Лист 1 из 4

М б/м

Кырлан Александр Сергеевич

Чек-лист приёмки по этапам. Лист 2 из 4

По этапам Р-1…Р-N: что проверить, чем, какой допуск и какой акт подписать до закрытия работы

Приёмка по этапам: контрольные точки, допуски и акты скрытых работ (продолжение)

Этап	Контрольная точка (дальше не пускают без подписи)	Что проверяют	Чем	Допуск	Основание	Подпись	Акт скрытых работ / документ
		Отметки выводов и положение инсталляций до зашивки и гидроизоляции	рулетка в кадре, фото	по листу выводов	практика		
Р-6	Штукатурка Маяки стен проверены до штукатурки; коробки скрытых дверей стоят до штукатурки	Отклонение от вертикали (простая / улучшенная / высококачественная штукатурка)	отвес, лазерный уровень	3 / 2 / 1 мм на 1 м; не более 15 / 10 / 5 мм на высоту	практика (СП 71.13330.2017)		Фото коробок скрытых дверей с отметкой чистого пола — до штукатурки; класс штукатурки (простая / улучшенная / высококачественная) назван в договоре.
		Отклонение от горизонтали	уровень, правило	3 / 2 / 1 мм на 1 м; не более 15 / 10 / 5 мм на длину	практика (СП 71.13330.2017)		
		Неровности (плоскостность)	правило 2 м и щуп	до 5 / 3 / 2 мм на 1 м; не более 3 / 2 / 2 неровностей на 4 м²	практика (СП 71.13330.2017)		
		Влажность основания перед шпаклёвкой и отделкой	влагомер	верхние 20–30 мм — не более 5 % по массе	норматив (СП 71, табл. 7.2)		
Р-7	Стяжка Стяжка: подготовка, после заливки ровность, затем замер СМ перед чистовым полом	Ровность: просвет под рейкой 2 м	рейка 2 м, клиновой щуп	под паркет, ламинат — 2 мм; под гидроизоляцию до 4 мм; прочие покрытия — до 6 мм (цифры расходятся между источниками — сверить перед актом)	практика (СП 29.13330)		Акт скрытых работ на стяжку (толщина, армирование) до чистового пола; протокол ровности и протокол СМ-влажности; звукоизоляция и демпферная лента под стяжкой — фото и паспорт; контуры тёплого пола до заливки — схема укладки и замер сопротивления.
		Отклонение от горизонтали по помещению	уровень, нивелир	не более 0,2 % длины помещения	практика (СП 29.13330)		
		Число точек измерения	рейка	не менее 3 на 30 м² или 1 на небольшое помещение	практика		
		Отслоения и пустоты	простукивание молотком или киянкой	глухой звук — зона вскрывается и переделывается	практика		
		Влажность перед укладкой доски: цементная стяжка	влагомер; СМ-замер	ЦПС не более 2,0 % СМ (с тёплым полом не более 1,8 %); влагомер для плитки — не более 5 %	практика (СП 71; рекомендации производителей)		
Р-8	Гидроизоляция Гидроизоляция: пролив 24 ч подпись до плитки	Заведение на стены не ниже 200 мм от чистого пола; за ванной — 300 мм выше борта; в душе без поддона — на высоту лейки	рулетка	не менее 200 мм	норматив (СП 71.13330.2017, п. 8.6.5); остальное — практика		Акт теста проливом, фото узлов и высоты заведения на стены — до плитки.
		Тест проливом: слой воды 10–30 мм, контроль уровня и потолка соседа снизу	линейка, визуально	24 ч (минимум 12 ч); падения уровня и протечки нет	практика		
		Два слоя обмазки с межслойной сушкой, лента в углах и манжеты на выводах	визуально	по инструкции производителя	практика		
Р-9	ГКЛ Короба, ниши и потолки: черновые сети в зоне коробов приняты до обшивки	Шаг саморезов, отступ от кромки, заделка стыков (как у перегородок)	рулетка, визуально	потолок 150 мм; кромка 5–10 мм; стык — лента и 2 слоя шпаклёвки	практика (СП 163.1325800.2014)		Акт скрытых работ: каркас ГКЛ, закладные, звукоизоляция — фото до обшивки; воздуховоды в коробах и за потолком — фото и схема.

Допущения и предложения на листе

Основа листа: размеры сняты со скана плана заказчика по размерным цепочкам, контрольный обмер на объекте не выполнялся (К-13); высота потолка 2700 мм принята: на плане заказчика не указана (К-11); толщины стен приняты: наружные 250 мм, перегородки 150 мм (на плане 85–190 мм) (К-13); разрешённая мощность 15 кВт принята по типовой квартире, технических условий нет (К-14); утолщение стены 190 × 1360 мм и элемент 1470 × 160 мм плана заказчика не определены (К-12); ниши санузла 2 закрыты перегородкой и фальш-стеной: проектное решение, на плане заказчика ниша у входа открыта (К-18); несущие стены не определены: до технического заключения все существующие стены считаются несущими (К-20); окна существующие и сохраняются; подоконная доска и глубина откосов не заданы — приняты, не замерены (К-27); подрайон климата не задан — принят не северный (жилые от 2,5 м) (К-29).

См. лист открытых вопросов (лист 7, записи К-11–К-14, К-18, К-20; лист 8, записи К-27, К-29).

Изм.	Кол.уч	Лист	№ док.	Подп.	Дата
Разраб.		Кырлан А.С.			13.11.26
Пров.					
ГИП					
Н. контр.					
Утв.					

ГД-2026-003-АИ

Трёхкомнатная квартира

Общая площадь 78,95* м² · * размеры со скана, не замерены (реестр — л. 6–11, К-13)

Дизайн-проект интерьера трёхкомнатной квартиры

Стадия	Лист	Листов
РП	23	132

Чек-лист приёмки по этапам. Лист 2 из 4

М б/м

Кырлан Александр Сергеевич

выпуск 13.11.2026 № 6f3a8abb2c · стр. 23 из 157

Чек-лист приёмки по этапам. Лист 3 из 4

По этапам Р-1…Р-N: что проверить, чем, какой допуск и какой акт подписать до закрытия работы

Приёмка по этапам: контрольные точки, допуски и акты скрытых работ (продолжение)

Этап	Контрольная точка (дальше не пускают без подписи)	Что проверяют	Чем	Допуск	Основание	Подпись	Акт скрытых работ / документ
		Закладные под тяжёлое, карнизы, подвесные светильники на месте до обшивки	фото с привязками	по плану потолков и узлам	практика		
		Ревизионные люки: доступ к арматуре и ревизиям сохранён	осмотр	по листу ВК	практика		
Р-10	Плитка Раскладка плитки: первая плита и первый ряд проверены по развёртке; плитка выбрана, калибр партии измерен	Уступы между смежными плитками	линейка, на просвет	не более 1 мм	норматив (СП 71.13330.2017)		Раскладка подписана до начала плитки; протокол первого ряда; акт теста проливом приложен (этап гидроизоляции).
		Ширина шва и его прямолинейность	линейка, калибр	до 6 мм ручная укладка; фактическая по проекту ±0,5 мм	практика		
		Отклонение рядов от вертикали и горизонтали	уровень, правило, отвес	1,5 мм на 1 м длины	практика		
		Ровность облицовки	правило 2 м и щуп	не более 2–4 мм (цифра расходится по источникам)	практика		
		Пустоты под плиткой	простукивание всей площади	до 10 % площади допустимо; свыше 25 % под одной плиткой — брак	практика		
Р-11	Шпаклёвка Шпаклёвка Q3/Q4: проверка боковым светом до окраски	Класс основания под окраску: Q3 — сплошное финишное шпаклевание; Q4 — под направленный свет	переносной прожектор у поверхности под острым углом	Q3: царапины от абразива до 0,5 мм; Q4 — без видимых царапин и теней; неровность на 2 м: Q3 — 1 мм, Q4 — 0,5 мм	практика (Q-классы — не норматив СП, а согласованный критерий)		Класс (Q3 или Q4) назван в договоре; грунтование и армирование стыков перед шпаклёвкой — запись в журнале.
Р-12	Окраска Выкрасы утверждены, колеровка одной партией	Окраска без полос, подтёков, пропусков; цвет — по колерной карте	боковой свет, образец выкраса	без видимых дефектов при боковом свете	практика		Утверждённые выкрасы; остаток колеровки одной партии — для подкраски.
		Основание сухое, огрунтованное; защита от прямого солнца при высыхании	осмотр	по ТУ краски	норматив (СП 71.13330.2017, п. 7.5.2)		
Р-13	Чистовые полы Чистовые полы: влажность, ровность, уступы, зазоры — до укладки доски; мокрые работы закончены	Деформационный зазор у стен и порогов (доска, ламинат)	линейка, клинья при укладке	8–15 мм (чаще 10 мм); у ламината 5–10 мм по СП 71	практика (требования производителей); норматив (СП 71, п. 8.10.14)		Протокол СМ-влажности стяжки до укладки; паспорт и партия доски.
		Перепад основания под покрытие	правило 2 м и щуп	не более 2 мм на 2 м	практика		
		Зазоры и перепады между досками; скрип; видимый зазор в замке — брак	щуп, рука, шаг	«ступеньки» нет	практика		
		Влажность помещения при укладке и после	гигрометр	не более 60 %, без сквозняков	норматив (СП 71, п. 8.1.7)		

Допущения и предложения на листе

Основа листа: размеры сняты со скана плана заказчика по размерным цепочкам, контрольный обмер на объекте не выполнялся (К-13); высота потолка 2700 мм принята: на плане заказчика не указана (К-11); толщины стен приняты: наружные 250 мм, перегородки 150 мм (на плане 85–190 мм) (К-13); разрешённая мощность 15 кВт принята по типовой квартире, технических условий нет (К-14); утолщение стены 190 × 1360 мм и элемент 1470 × 160 мм плана заказчика не определены (К-12); ниши санузла 2 закрыты перегородкой и фальш-стеной: проектное решение, на плане заказчика ниша у входа открыта (К-18); несущие стены не определены: до технического заключения все существующие стены считаются несущими (К-20); окна существующие и сохраняются; подоконная доска и глубина откосов не заданы — приняты, не замерены (К-27); подрайон климата не задан — принят не северный (жилые от 2,5 м) (К-29).

См. лист открытых вопросов (лист 7, записи К-11–К-14, К-18, К-20; лист 8, записи К-27, К-29).

Изм.	Кол.уч	Лист	№ док.	Подп.	Дата
Разраб.		Кырлан А.С.			13.11.26
Пров.					
ГИП					
Н. контр.					
Утв.					

ГД-2026-003-АИ

Трёхкомнатная квартира

Общая площадь 78,95* м² · * размеры со скана, не замерены (реестр — л. 6–11, К-13)

Дизайн-проект интерьера трёхкомнатной квартиры

Стадия	Лист	Листов
РП	24	132

Чек-лист приёмки по этапам. Лист 3 из 4

М б/м

Кырлан Александр Сергеевич

выпуск 13.11.2026 № 6f3a8abb2c · стр. 24 из 157

Чек-лист приёмки по этапам. Лист 4 из 4

По этапам Р-1…Р-N: что проверить, чем, какой допуск и какой акт подписать до закрытия работы

Приёмка по этапам: контрольные точки, допуски и акты скрытых работ (продолжение)

Этап	Контрольная точка (дальше не пускают без подписи)	Что проверяют	Чем	Допуск	Основание	Подпись	Акт скрытых работ / документ
Р-14	Двери и плинтусы Полотна и плинтусы — после чистового пола; скрытые полотна после чистовой отделки стен	Отклонение коробки от вертикали	отвес, уровень	1,5 мм на 1 м, не более 3 мм на коробку	практика (ТР 105-00, пересказ)		Коробки скрытых дверей приняты до штукатурки (этап штукатурки); паспорт на полотна.
		Зазор между полотном и коробкой по периметру	щуп	2–4 мм по бокам и верху (единого норматива нет)	практика		
		Открывание и закрывание: без перекоса, плавный ход петель и доводчика	визуально, от руки	без задевания коробки и пола	практика		
Р-15	Чистовая электрика и сантехника Чистовая электрика и сантехника: протокол электролаборатории и проверка УЗО до подписи акта	УЗО: кнопка «Тест»; время отключения; ток отключения	кнопка на аппарате; прибор проверки УЗО (не мультиметр)	отключает; не более 0,3 с; 50–100 % от IΔn	практика измерений		Протокол измерений аккредитованной электролаборатории (изоляция по группам, УЗО, PE, фаза-ноль); исполнительная схема щита; акт опрессовки приложен (этап ВК).
		Сопротивление изоляции готовых линий; петля фаза-ноль для срабатывания автоматов	мегаомметр; прибор петли фаза-ноль	изоляция не менее 0,5 МОм; петля — по проекту	норматив (ПУЭ, гл. 1.8) / по проекту		
		Смесители, сифоны, гибкая подводка: пробный пуск воды	визуально под нагрузкой	нет подтёков в контрольное время	практика		
Р-16	Кухня и мебель Кухня и мебель: замер кухни снят по готовым стенам; чистовая электрика и сантехника подведены	Привязка выводов и розеток к модулям кухни; вытяжка, вентиляция	рулетка, сверка с листом кухни	по проекту кухни	практика		Акт передачи кухни; паспорта техники и гарантийные талоны.
		Тяга вентиляции у решёток	лист бумаги у решётки	бумага притягивается; при сомнениях — замер анемометром	практика		
Р-17	Сдача Финальная приёмка по таблицам СП 71: дефектная ведомость и акт	Стены, потолки, полы, плитка, двери, окна осмотр по чек-листу этапов выше	правило 2 м, уровень, щуп, боковой свет, влагомер	по таблицам выше	практика		Дефектная ведомость и акт приёмки; гарантия: по умолчанию претензии по качеству работ — 2 года, в договоре прописывается отдельно.
		Полный пакет документов: акты скрытых работ, протокол электролаборатории, акт опрессовки, исполнительные схемы, гарантийные обязательства	комплектность	пакет собран до подписи акта	практика		

Примечания

1. Метка основания: «норматив» — цифра подтверждена текстом СП, ГОСТ или ПУЭ; «практика» — отраслевая конвенция или один источник: к спору не годится без сверки первоисточника (СП 71.13330.2017, СП 29.13330, СП 163.1325800.2014, ПУЭ гл. 1.8, СП 73.13330, СП 30.13330).
2. Класс штукатурки (простая / улучшенная / высококачественная) и класс основания под окраску (Q3 или Q4) называются в договоре подряда: допуск выбирается по ним. Q-классы — не норматив, а согласованный сторонами критерий.
3. Акт скрытых работ подписывают до того, как работа закрыта следующим слоем (штукатуркой, плиткой, стяжкой, обшивкой): постфактум он слабее — осматривать нечего. Подписывают заказчик (или технадзор), подрядчик; при перепланировке — автор проекта. Каждую зону снимают до закрытия с рулеткой в кадре и привязкой к стене.
4. По умолчанию, если срок не прописан в договоре, претензии по качеству работ можно предъявить в течение 2 лет со дня приёмки; в договоре гарантийный срок и сроки на скрытые работы рекомендуется назвать явно.

Допущения и предложения на листе

Основа листа: размеры сняты со скана плана заказчика по размерным цепочкам, контрольный обмер на объекте не выполнялся (К-13); высота потолка 2700 мм принята: на плане заказчика не указана (К-11); толщины стен приняты: наружные 250 мм, перегородки 150 мм (на плане 85–190 мм) (К-13); разрешённая мощность 15 кВт принята по типовой квартире, технических условий нет (К-14); утолщение стены 190 × 1360 мм и элемент 1470 × 160 мм плана заказчика не определены (К-12); ниши санузла 2 закрыты перегородкой и фальш-стеной: проектное решение, на плане заказчика ниша у входа открыта (К-18); несущие стены не определены: до технического заключения все существующие стены считаются несущими (К-20); окна существующие и сохраняются; подоконная доска и глубина откосов не заданы — приняты, не замерены (К-27); подрайон климата не задан — принят не северный (жилые от 2,5 м) (К-29).

См. лист открытых вопросов (лист 7, записи К-11–К-14, К-18, К-20; лист 8, записи К-27, К-29).

Изм.	Кол.уч	Лист	№ док.	Подп.	Дата
Разраб.		Кырлан А.С.			13.11.26
Пров.					
ГИП					
Н. контр.					
Утв.					

ГД-2026-003-АИ

Трёхкомнатная квартира

Общая площадь 78,95* м² · * размеры со скана, не замерены (реестр — л. 6–11, К-13)

Дизайн-проект интерьера трёхкомнатной квартиры

Стадия	Лист	Листов
РП	25	132

Чек-лист приёмки по этапам. Лист 4 из 4

М б/м

Кырлан Александр Сергеевич

Лист → мастер

Мастер → листы альбома и документы, которые ему нужны

Какому мастеру какие листы (номера — как в штампе)

Мастер	Что делает по альбому	Листы	Кроме чертежей — документы	Листов
Замерщик и прораб (до начала работ)	Контрольный обмер на голых стенах, сверка размеров и диагоналей, ответы на открытые вопросы до заказа	2–16, 27	Задание на контрольный обмер; лист открытых вопросов	16
Гипсокартонщик и монтажник перегородок	Демонтаж и возведение перегородок, каркас, короба инсталляции, ниши, потолки; закладные под навесное	28–29, 58–61, 83, 85	Ведомость материалов каркаса; акт скрытых работ на каркас	8
Электрик	Группы щита, подрозетники и высоты, трассы, свет, управление светом, слаботочка, тёплый пол	37–45, 57, 89–113	Таблица нагрузок; ведомость изделий; протокол электролаборатории	35
Сантехник	Выводы воды и канализации, разводка, аксонометрии, инсталляции, короба стояков	48–56, 89–113	Спецификация ВК; акт опрессовки; акт пролива	34
Монтажник вентиляции, отопления и кондиционеров	Вентиляция, радиаторы и тёплые полы, кондиционеры: места, размеры, трассы и дренаж	46–47	Акт опрессовки азотом (кондиционеры); фото воздуховодов до закрытия	2
Штукатур, шпаклёвщик, маляр, паркетчик	Основание стен, окраска и обои по колерной карте, полы и пороги, плинтус, узлы стыков	66–70, 89–115	Колерная карта и выкрасы; спецификация отделочных материалов	32
Плиточник	Раскладка и подрезка плитки стен, пола и фартука, гидроизоляция, швы, выводы в плитке	53–55, 62–65, 89–115	Ведомость плитки; акт теста проливом	34
Монтажник дверей и окон	Заполнение проёмов: размеры коробок, открывание, пороги, скрытые двери	30	Ведомость проёмов; паспорта на полотна	1
Мебельщик, кухонный монтажник	Кухня и мебель на заказ: габариты, членение, фурнитура, связка с электрикой и сантехникой	32–36, 77–87	Ведомость изделий; замер кухни по готовым стенам	16
Заказчик и комплектатор	Что и когда покупать, сколько с запасом, во что это обойдётся; свет, декор и текстиль; визуализации как должно получиться	1, 17–21, 57, 71–72, 75–76, 116–132	Список покупок; смета; календарный график	28
Прораб и технадзор (приёмка)	Приёмка этапов, акты скрытых работ, дефектная ведомость	21–26	Чек-лист приёмки по этапам; календарный график	6

Примечания

1. Номера листов — как в основной надписи: основные подряд (1, 2, 3…), «Д» — детализация мебели, «С» — ведомости, спецификации, узлы и сметы, «П» — приложение единого комплекта. «12–18» — все листы с 12 по 18.
2. Лист может быть у нескольких мастеров: развёртка стены нужна электрику (высоты точек), сантехнику (выводы), отделочнику (материалы) и плиточнику (раскладка). Общие листы (обмер, список листов, перечень вопросов) прораб раздаёт всем.
3. Мастер работает по чертежам и берёт в руки то, что назначено ему здесь; закупки, смету и график ведёт заказчик с прорабом. Лист, которого нет в таблице ни у одного мастера, — вопрос прорабу: чей он.

Допущения и предложения на листе

Основа листа: размеры сняты со скана плана заказчика по размерным цепочкам, контрольный обмер на объекте не выполнялся (К-13); высота потолка 2700 мм принята: на плане заказчика не указана (К-11); толщины стен приняты: наружные 250 мм, перегородки 150 мм (на плане 85–190 мм) (К-13); разрешённая мощность 15 кВт принята по типовой квартире, технических условий нет (К-14); утолщение стены 190 × 1360 мм и элемент 1470 × 160 мм плана заказчика не определены (К-12); ниши санузла 2 закрыты перегородкой и фальш-стеной: проектное решение, на плане заказчика ниша у входа открыта (К-18); несущие стены не определены: до технического заключения все существующие стены считаются несущими (К-20); окна существующие и сохраняются; подоконная доска и глубина откосов не заданы — приняты, не замерены (К-27); подрайон климата не задан — принят не северный (жилые от 2,5 м) (К-29).

См. лист открытых вопросов (лист 7, записи К-11–К-14, К-18, К-20; лист 8, записи К-27, К-29).

Изм.	Кол.уч	Лист	№ док.	Подп.	Дата
Разраб.		Кырлан А.С.			13.11.26
Пров.					
ГИП					
Н. контр.					
Утв.					

ГД-2026-003-АИ

Трёхкомнатная квартира

Общая площадь 78,95* м² · * размеры со скана, не замерены (реестр — л. 6–11, К-13)

Дизайн-проект интерьера трёхкомнатной квартиры

Стадия	Лист	Листов
РП	26	132

Лист → мастер

М б/м

Кырлан Александр Сергеевич

выпуск 13.11.2026 № 6f3a8abb2c · стр. 26 из 157

01

Архитектурные решения



Кырлан Александр Сергеевич

выпуск 13.11.2026 № 6f3a8abb2c · стр. 27 из 157


Обмерный план

Существующее положение · размеры в мм · отметки от чистого пола

ПРЕДВАРИТЕЛЬНО · не для производства работ · открыто пунктов: 28 (реестр — л. 6–11)

Отметки по высоте

±0,000	чистый пол пом. 1, 3–6, 8; отсчёт высот
−0,015	чистый пол пом. 2, 7, ниже на 15 мм
−0,064*	верх плиты — расчёт, не замер (К-13)
сущ. пол	снимается до плиты; не замерен (К-13)

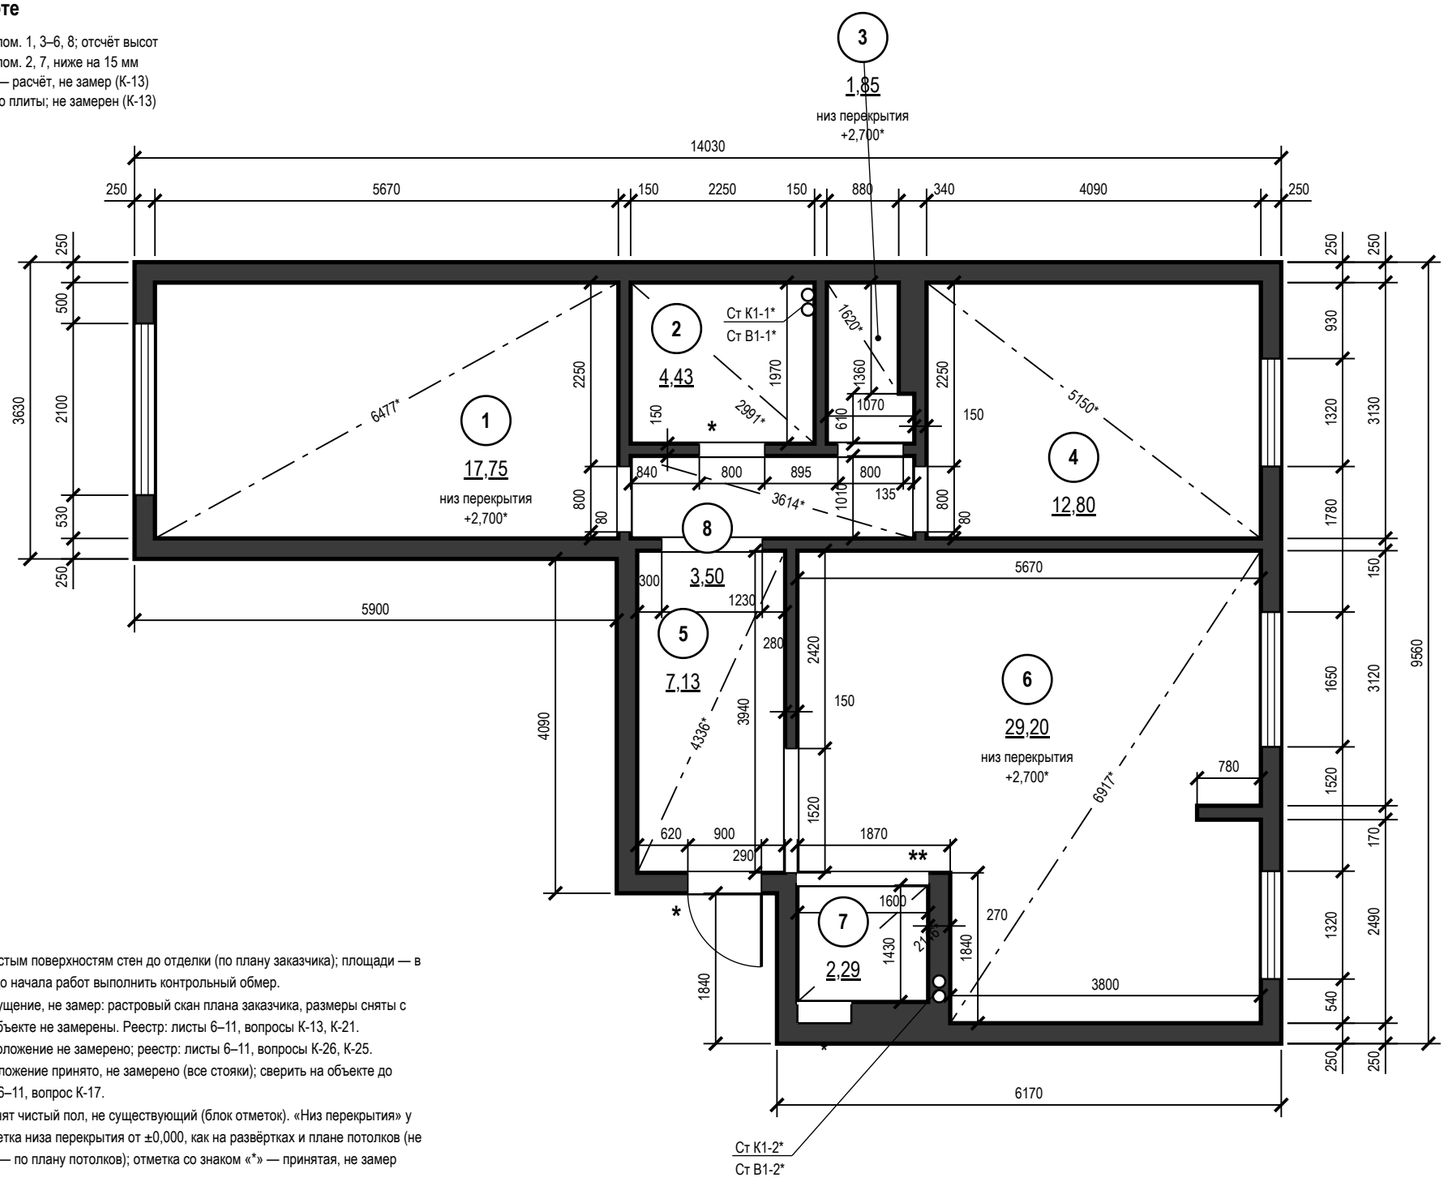

Экспликация помещений

№	Наименование	Площадь, м²
1	Спальня 1	17,75
2	Ванная	4,43
3	Гардеробная	1,85
4	Спальня 2	12,80
5	Прихожая	7,13
6	Кухня-гостиная	29,20
7	Санузел 2	2,29
8	Коридор	3,50
	Итого (общая площадь)	**78,95**

Условные обозначения

- существующие стены (сечение)
- окно (рама, остекление)
- проём существующий, без заполнения (откосы)
- стояк: К1 — канализация, В1 — ХВС, Т3 — ГВС
- ** — «**» — предложение проектировщика, заказчиком не утверждено
- ниша в стене — существующая пустота
- диагональ помещения — контроль прямоугольности
- (1) — номер помещения, площадь м²
- * — «*» — принято, не замерено и не подтверждено

Примечания

1. Размеры — в мм по чистым поверхностям стен до отделки (по плану заказчика); площади — в м² по тем же размерам. До начала работ выполнить контрольный обмер.
2. Источник плана — допущение, не замер: растровый скан плана заказчика, размеры сняты с размерных цепочек, на объекте не замерены. Реестр: листы 6–11, вопросы К-13, К-21.
3. Знак «*» у проёма — положение не замерено; реестр: листы 6–11, вопросы К-26, К-25.
4. Знак «*» у стояка — положение принято, не замерено (все стояки); сверить на объекте до разметки. Реестр: листы 6–11, вопрос К-17.
5. За отметку ±0,000 принят чистый пол, не существующий (блок отметок). «Низ перекрытия» у марки помещения — отметка низа перекрытия от ±0,000, как на развёртках и плане потолков (не высота потолка: потолок — по плану потолков); отметка со знаком «*» — принятая, не замер (вопрос К-11).
6. Толщины стен: наружные 250 мм, перегородки 150 мм — приняты, не замерены (вопрос К-13); отличающиеся толщины и уступы — размерами на плане.
7. Обмер — существующее положение: новых конструкций на листе нет, они — на плане монтажа.
8. Несущие стены не определены: до технического заключения все стены считать несущими; проёмы и штробы в них не выполнять.
9. Дверные проёмы показаны без заполнения (двери — лист 30); высота дверных проёмов 2100 мм, проёмов без двери 2500, 2100 мм; низ окон (подоконник) 900 мм от чистого пола, высота окон 1500, 1400 мм.
10. Диагонали — контрольные размеры; «*» — расчёт по принятому контуру (К-13), при обмере заменить замеренным; расхождение более 5 мм подписать на плане как перекос.
11. Размеры проверить на месте до начала работ; расхождение контрольных промеров ≤ 2 %.

Принято, не определено или спорно

полностью — листы 6–11

К-4 — Вход в санузел 2 (с унитазом) — из кухни-гостиной: так по плану заказчика (ниша у входа на плане открыта в кухню-гостиную, в проекте закрыта перегородкой по линии низа прихожей)

К-12 — Две конструкции плана заказчика не определены: утолщение стены 190 × 1360 мм в гардеробной у спальни 2 (вентблок или пилон) и элемент 1470 × 160 мм на линии простенка кухни-гостиной (пилон, балка или барная стойка)

Допущения и предложения на листе. Основа листа: размеры сняты со скана плана заказчика по размерным цепочкам, контрольный обмер на объекте не выполнялся (К-13); высота потолка 2700 мм принята: на плане заказчика не указана (К-11); толщины стен приняты: наружные 250 мм, перегородки 150 мм (на плане 85–190 мм) (К-13); разрешённая мощность 15 кВт принята по типовой квартире, технических условий нет (К-14); утолщение стены 190 × 1360 мм и элемент 1470 × 160 мм плана заказчика не определены (К-12); ниши санузла 2 закрыты перегородкой и фальш-стеной: проектное решение, на плане заказчика ниша у входа открыта (К-18); несущие стены не определены: до технического заключения все существующие стены считаются несущими (К-20); окна существующие и сохраняются; подоконная доска и глубина откосов не заданы — приняты, не замерены (К-27); подрайон климата не задан — принят не северный (жилые от 2,5 м) (К-29). Знак «*» — принято, не замерено (замерить): К-13: отметка существующего пола; К-25: дверь пом. 8 (стена А). Знак «**» — предложено, не утверждено (согласовать). См. лист открытых вопросов (лист 6, запись К-4; лист 7, записи К-11–К-14, К-17, К-18, К-20, К-21; лист 8, записи К-25–К-27, К-29).

1000 мм · печать 1:1

Изм.	Кол.уч	Лист	№ док.	Подп.	Дата
Разраб.		Кырлан А.С.			13.11.26
Пров.					
ГИП					
Н. контр.					
Утв.					

ГД-2026-003-АИ

Трёхкомнатная квартира

Общая площадь 78,95* м² · * размеры со скана, не замерены (реестр — л. 6–11, К-13)

Дизайн-проект интерьера трёхкомнатной квартиры

Стадия	Лист	Листов
РП	27	132

Обмерный план

М 1:75


Кырлан Александр Сергеевич

выпуск 13.11.2026 № 6f3a8abb2c · стр. 28 из 157

План демонтажа и монтажа перегородок

Существующее — серым, демонтаж — красным, монтаж — синим · размеры в мм

ПРЕДВАРИТЕЛЬНО · не для производства работ · открыто пунктов: 28 (реестр — л. 6–11)

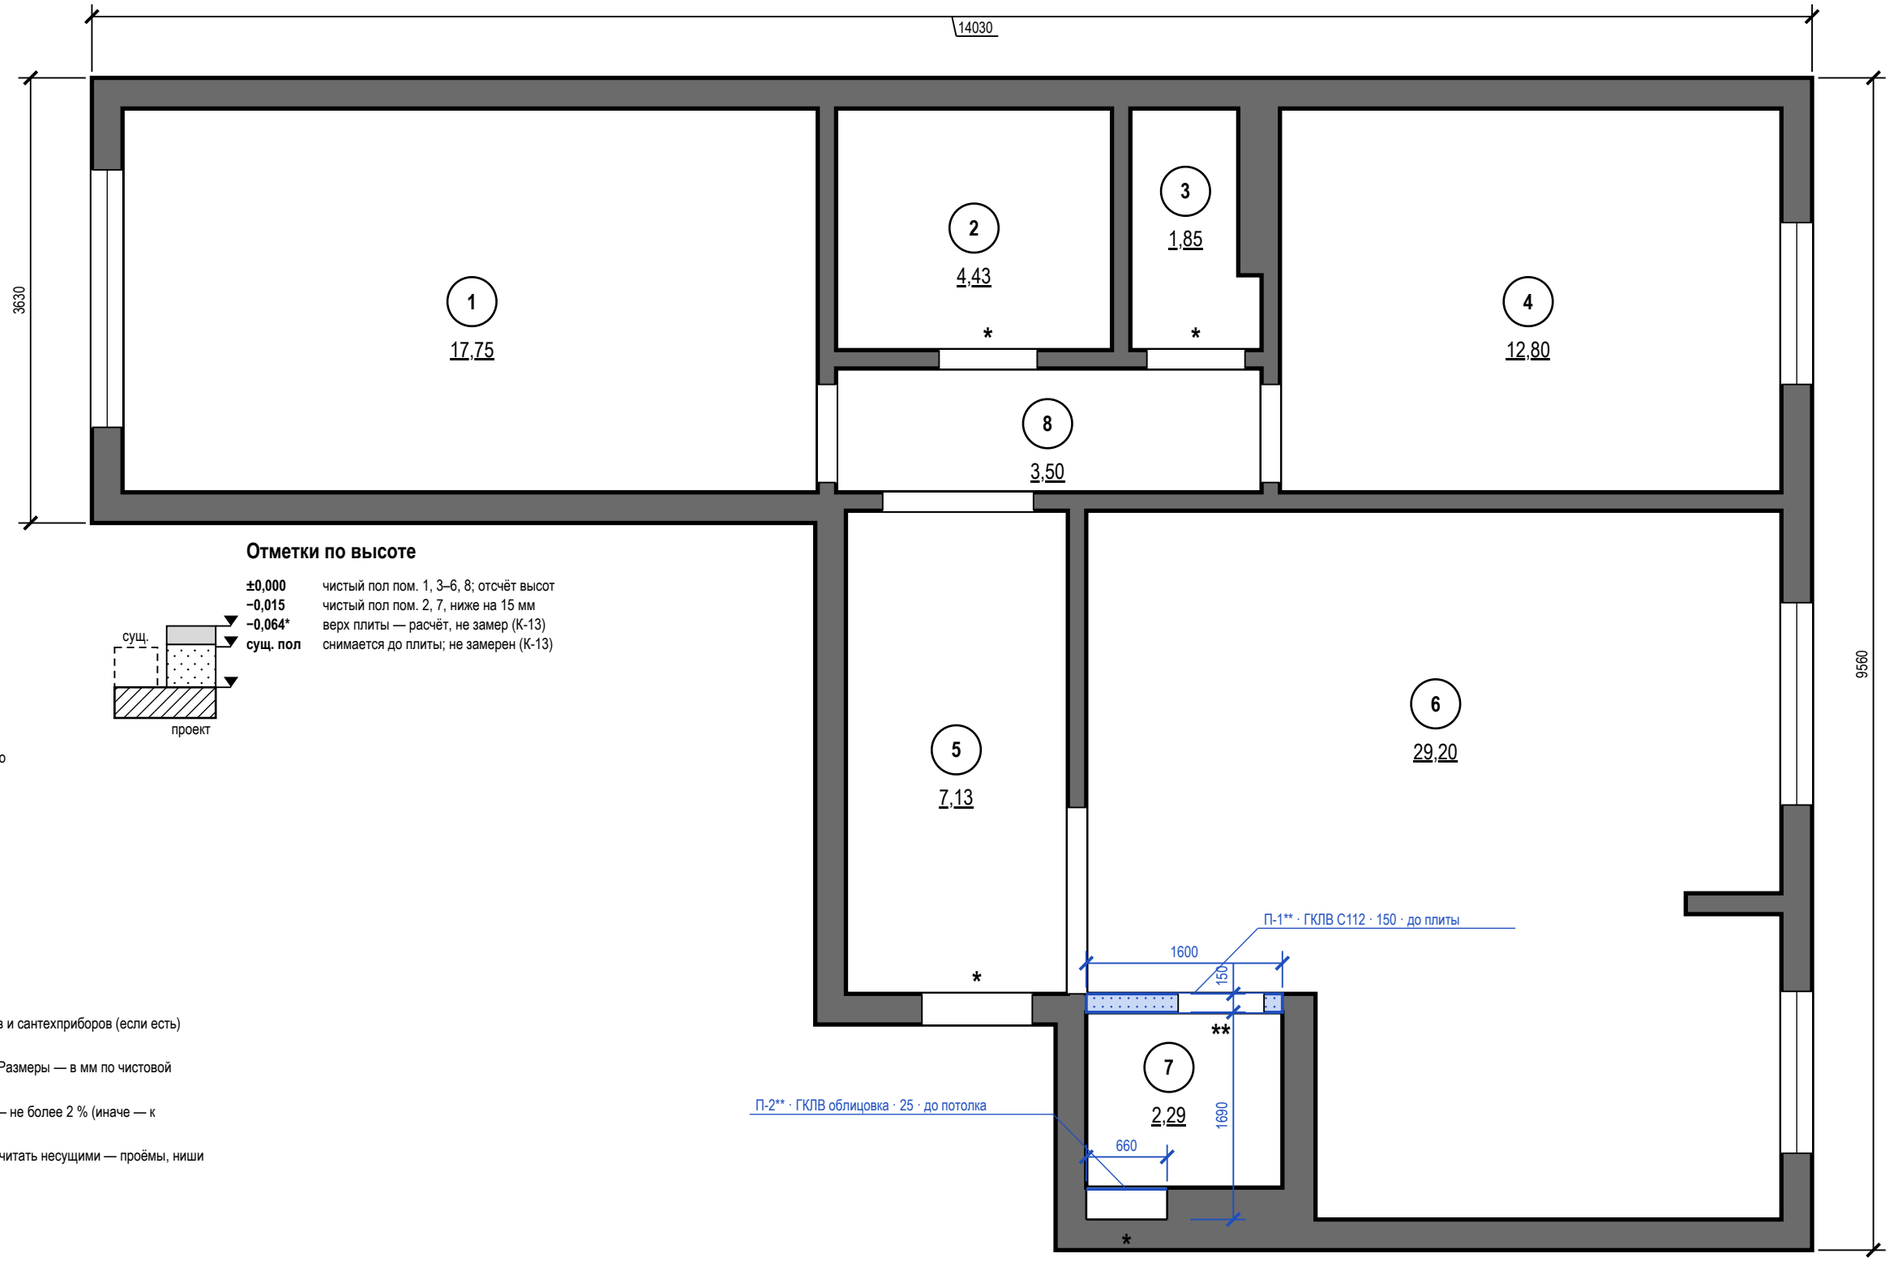

Условные обозначения

- существующие стены — сохраняются; несущие не определены — считать несущими
- демонтируемые конструкции — на плане нет
- новое — возводится по проекту (синим)
- ** — «**» — предложение проектировщика, заказчиком не утверждено
- ниша в стене — существующая пустота
- проём существующий, без заполнения (откосы)
- (1) — номер помещения, площадь м²
- * — «*» — принято, не замерено и не подтверждено

Отметки по высоте

±0,000	чистый пол пом. 1, 3–6, 8; отсчёт высот
−0,015	чистый пол пом. 2, 7, ниже на 15 мм
−0,064*	верх плиты — расчёт, не замер (К-13)
сущ. пол	снимается до плиты; не замерен (К-13)

Примечания

1. Демонтаж несущих стен и плит перекрытия не производится.
2. Демонтаж существующих покрытий пола, стен и потолка, дверных блоков и сантехприборов (если есть) — до основания; объёмы демонтажа — для справки, по факту на объекте.
3. За отметку ±0,000 принят чистый пол, не существующий (блок отметок). Размеры — в мм по чистовой поверхности стен до отделки.
4. Размеры проверить на месте до начала работ: расхождение с обмером — не более 2 % (иначе — к архитектору).
5. Несущие стены не определены: до технического заключения все стены считать несущими — проёмы, ниши и штробы в них не выполнять.
6. Ведомость демонтажа и монтажа и остальные примечания — лист 29.

Допущения и предложения на листе. Основа листа: размеры сняты со скана плана заказчика по размерным цепочкам, контрольный обмер на объекте не выполнялся (К-13); высота потолка 2700 мм принята: на плане заказчика не указана (К-11); толщины стен приняты: наружные 250 мм, перегородки 150 мм (на плане 85–190 мм) (К-13); разрешённая мощность 15 кВт принята по типовой квартире, технических условий нет (К-14); утолщение стены 190 × 1360 мм и элемент 1470 × 160 мм плана заказчика не определены (К-12); ниши санузла 2 закрыты перегородкой и фальш-стеной: проектное решение, на плане заказчика ниша у входа открыта (К-18); несущие стены не определены: до технического заключения все существующие стены считаются несущими (К-20); окна существующие и сохраняются; подоконная доска и глубина откосов не заданы — приняты, не замерены (К-27); подрайон климата не задан — принят не северный (жилые от 2,5 м) (К-29). Знак «*» — принято, не замерено и не подтверждено (замерить на объекте): К-13: отметка существующего пола — отметка существующего пола и верха плиты не замерена: на плане заказчика отметок нет; нивелировка — в задании на обмер (К-13). Знак «**» — предложение проектировщика, заказчиком не утверждено (согласовать с заказчиком): К-4, К-18: П-1 — проектное решение исполнителя: на плане заказчика ниша у входа открыта в кухню-гостиную; конструкция не утверждена автором (вопрос К-18), положение и размеры сняты со скана (К-13); К-18: П-2 — проектное решение исполнителя: на плане заказчика у наружной стены уступ 660 × 260 мм; конструкция не утверждена автором (вопрос К-18). См. лист открытых вопросов (лист 6, запись К-4; лист 7, записи К-11–К-14, К-18, К-20; лист 8, записи К-25–К-27, К-29); по листу — К-20.

1000 мм · печать 1:1

Изм.	Кол.уч	Лист	№ док.	Подп.	Дата
Разраб.		Кырлан А.С.			13.11.26
Пров.					
ГИП					
Н. контр.					
Утв.					

ГД-2026-003-АИ

Трёхкомнатная квартира

Общая площадь 78,95* м² · * размеры со скана, не замерены (реестр — л. 6–11, К-13)

Дизайн-проект интерьера трёхкомнатной квартиры

Стадия	Лист	Листов
РП	28	132

План демонтажа и монтажа перегородок

М 1:50

Кырлан Александр Сергеевич

выпуск 13.11.2026 № 6f3a8abb2c · стр. 29 из 157

Ведомость демонтажа и монтажа перегородок

Демонтаж — красным, монтаж — синим (на плане) · размеры в мм

Ведомость демонтажа и монтажа

Марка	Конструкция	Длина, мм	Толщ., мм	Высота	Примечание
П-1**	монтаж: ГКЛВ 2 слоя с каждой стороны по металлическому каркасу ПС 100, С112	1600	150	до плиты, 2700	закрывает нишу 1600×1840; проём Д-5 700, обрамление УА; упор — наружная стена и пилон Ш2
П-2**	монтаж: фальш-стена (облицовка), ГКЛВ 2 слоя по раме инсталляции унитаза; лицевая плоскость по линии уступа стены, без системы Knauf	660	25	до потолка, 2389	закрывает нишу 660×260 у наружной стены; за ней рама инсталляции

Примечания

1. План демонтажа и монтажа в масштабе 1:50 — лист 28; марки в ведомости — те же, что на плане.
2. Демонтаж несущих стен и плит перекрытия не производится.
3. Новые перегородки и фальш-стены (синим) привязаны от капитальных стен и наружного контура; высота — по ведомости («до плиты» — до низа плиты перекрытия); проёмы в них усилить стойками каркаса.
4. Знак «**» — предложение проектировщика, заказчиком не утверждено (согласовать с заказчиком) у конструкций (вопросы К-18, К-4): до решения не возводить. На обмерном плане их нет.
5. Перепланировку согласовать до начала работ (ЖК РФ, ст. 26); план не передавать в работу до допуска главного инженера проекта.
6. Дверные блоки — по плану дверей (лист 30); существующие проёмы не расширяются.
7. Знак «*» — положение проёма не замерено: двери пом. 5, 8, 8. Реестр: листы 6–11, вопросы К-26, К-25.
8. Демонтаж существующих покрытий пола, стен и потолка, дверных блоков и сантехприборов (если есть) — до основания; объёмы демонтажа — для справки, по факту на объекте.
9. За отметку ±0,000 принят чистый пол, не существующий (блок отметок). Размеры — в мм по чистовой поверхности стен до отделки.
10. Размеры проверить на месте до начала работ: расхождение с обмером — не более 2 % (иначе — к архитектору).
11. Несущие стены не определены: до технического заключения все стены считать несущими — проёмы, ниши и штробы в них не выполнять.

Допущения и предложения на листе

Основа листа: размеры сняты со скана плана заказчика по размерным цепочкам, контрольный обмер на объекте не выполнялся (К-13); высота потолка 2700 мм принята: на плане заказчика не указана (К-11); толщины стен приняты: наружные 250 мм, перегородки 150 мм (на плане 85–190 мм) (К-13); разрешённая мощность 15 кВт принята по типовой квартире, технических условий нет (К-14); утолщение стены 190 × 1360 мм и элемент 1470 × 160 мм плана заказчика не определены (К-12); ниши санузла 2 закрыты перегородкой и фальш-стеной: проектное решение, на плане заказчика ниша у входа открыта (К-18); несущие стены не определены: до технического заключения все существующие стены считаются несущими (К-20); окна существующие и сохраняются; подоконная доска и глубина откосов не заданы — приняты, не замерены (К-27); подрайон климата не задан — принят не северный (жилые от 2,5 м) (К-29).

Знак «**» — предложение проектировщика, заказчиком не утверждено (согласовать с заказчиком): К-4, К-18: П-1 — проектное решение исполнителя: на плане заказчика ниша у входа открыта в кухню-гостиную; конструкция не утверждена автором (вопрос К-18), положение и размеры сняты со скана (К-13); К-18: П-2 — проектное решение исполнителя: на плане заказчика у наружной стены уступ 660 × 260 мм; конструкция не утверждена автором (вопрос К-18).

См. лист открытых вопросов (лист 6, запись К-4; лист 7, записи К-11–К-14, К-18, К-20; лист 8, записи К-27, К-29).

Изм.	Кол.уч	Лист	№ док.	Подп.	Дата
Разраб.		Кырлан А.С.			13.11.26
Пров.					
ГИП					
Н. контр.					
Утв.					

ГД-2026-003-АИ

Трёхкомнатная квартира

Общая площадь 78,95* м² · * размеры со скана, не замерены (реестр — л. 6–11, К-13)

Дизайн-проект интерьера трёхкомнатной квартиры

Стадия	Лист	Листов
РП	29	132

Ведомость демонтажа и монтажа перегородок

М б/м

Кырлан Александр Сергеевич

выпуск 13.11.2026 № 6f3a8abb2c · стр. 30 из 157

План дверей и ведомость заполнения проёмов

Проёмы, марки заполнения, привязки · размеры в мм

Допущения и предложения на листе. Основа листа: размеры сняты со скана плана заказчика по размерным цепочкам, контрольный обмер на объекте не выполнялся (К-13); высота потолка 2700 мм принята: на плане заказчика не указана (К-11); толщины стен приняты: наружные 250 мм, перегородки 150 мм (на плане 85–190 мм) (К-13); разрешённая мощность 15 кВт принята по типовой квартире, технических условий нет (К-14); утолщение стены 190 × 1360 мм и элемент 1470 × 160 мм плана заказчика не определены (К-12); ниши санузла 2 закрыты перегородкой и фальш-стеной: проектное решение, на плане заказчика ниша у входа открыта (К-18); несущие стены не определены: до технического заключения все существующие стены считаются несущими (К-20); окна существующие и сохраняются; подоконная доска и глубина откосов не заданы — приняты, не замерены (К-27); подрайон климата не задан — принят не северный (жилые от 2,5 м) (К-29). Знак «*» — принято, не замерено и не подтверждено (замерить на объекте): К-17: Ст К1-1, Ст В1-1, Ст К1-2, Ст В1-2. Знак «**» — предложение проектировщика, заказчиком не утверждено (согласовать с заказчиком): К-4, К-18: П-1 — проектное решение исполнителя: на плане заказчика ниша у входа открыта в кухню-гостиную; конструкция не утверждена автором (вопрос К-18), положение и размеры сняты со скана (К-13); К-18: П-2 — проектное решение исполнителя: на плане заказчика у наружной стены уступ 660 × 260 мм; конструкция не утверждена автором (вопрос К-18). См. лист открытых вопросов (лист 6, запись К-4; лист 7, записи К-11–К-14, К-17, К-18, К-20; лист 8, записи К-25–К-27, К-29); по листу — К-4, К-25–К-27.


Ведомость заполнения проёмов

Марка	Наименование, обозначение	Проём ш×в, мм	Полотно (расч.)	Кол.	Откр.	Отделка полотна	Фурнитура	Прим.
Д-1	Блок дверной входной, ГОСТ 31173-2016	900×2100	блок задать	1	П	в комплекте блока	в комплекте блока (замки, глазок)	* пом. 5; наружу
Д-2	Дверь скрытого монтажа, ТУ изготовителя	800×2100	700×2000	2	П, Л	окраска No. 241 с двух сторон	скрытые петли 3D, магнитный замок	б/п
Д-3	Дверь скрытого монтажа, ТУ изготовителя	800×2100	700×2000	1	Л	No. 241 — пом. 8, в тон облицовки — пом. 2	скрытые петли 3D, магнитный замок, фиксатор WC	* пом. 8; порог 15
Д-4	Дверь скрытого монтажа, ТУ изготовителя	800×2100	700×2000	1	П	No. 241 — пом. 8, V503 — пом. 3	скрытые петли 3D, магнитный замок	* пом. 8; б/п
Д-5	Дверь скрытого монтажа, ТУ изготовителя	700×2100	600×2000	1	П	No. 241 — пом. 6, в тон облицовки — пом. 7	скрытые петли 3D, магнитный замок, фиксатор WC	** пом. 6; порог 15
ПР-1	Портал без заполнения	1520×2500		1				
ПР-2	Портал без заполнения	1230×2100		1				
ОК-1	Блок оконный существующий	2100×1500		1				низ 900
ОК-2	Блок оконный существующий	1320×1500		1				низ 900
ОК-3	Блок оконный существующий	1650×1500		1				низ 900
ОК-4	Блок оконный существующий	1320×1400		1				низ 900

Условные обозначения

- стены (подложка обмера)
- новое — возводится по проекту (синим)
- дверь распашная, дуга открывания
- дверь скрытого монтажа
- дверь входная (полотно толще)
- портал (штрих — перемычка)
- оконный блок
- Д — марка типа (Д-N, ПР-N, ОК-N)
- 1 — номер помещения, площадь м²
- * — «*» — принято, не замерено и не подтверждено
- ** — «**» — предложение проектировщика, заказчиком не утверждено

1000 мм · печать 1:1

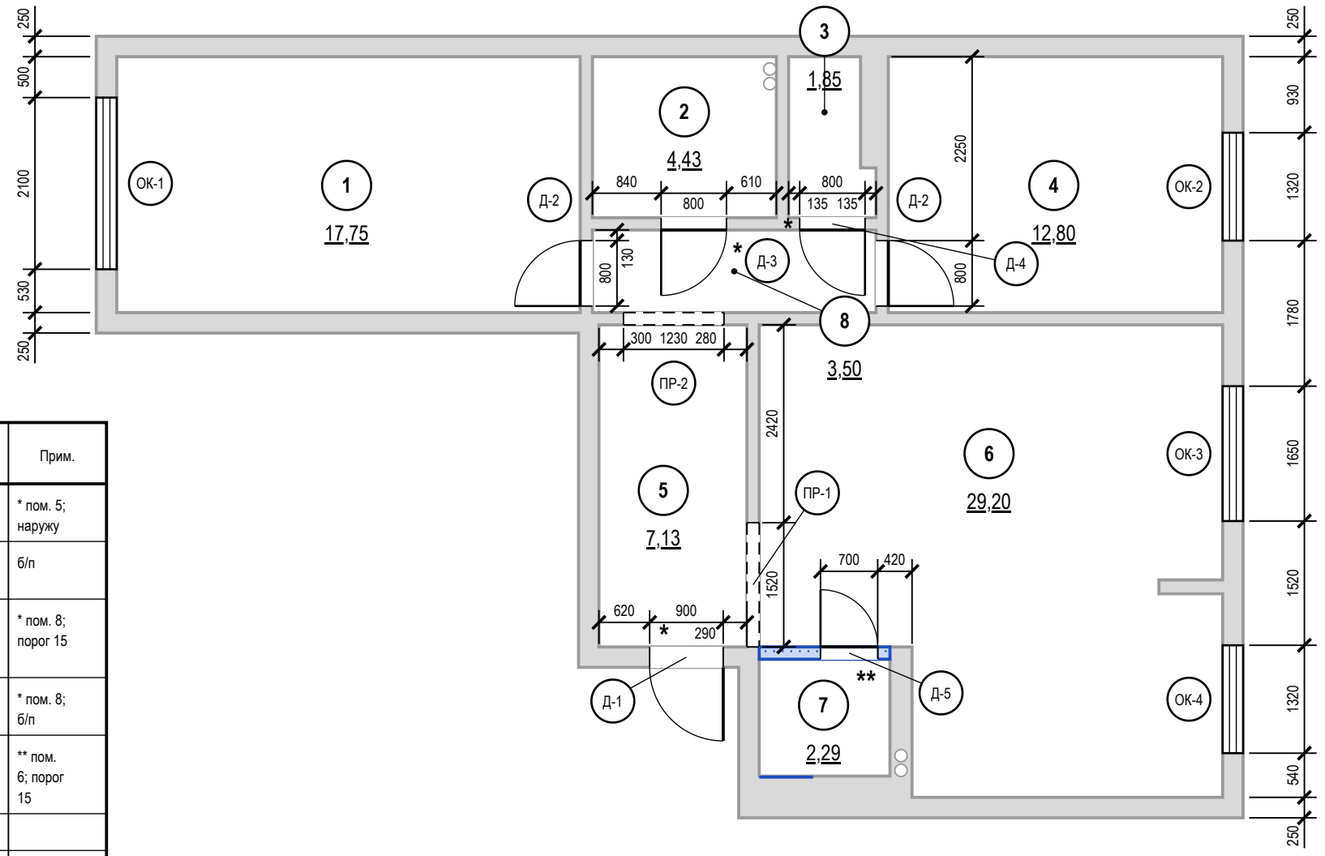

Примечания

1. Размеры проёмов и привязки — в миллиметрах от чистых граней стен до отделки; привязка — от угла того помещения, со стороны которого стоит размер. Размер проёма — ширина × высота от чистого пола 0,000. Размеры на плане — проёмов, не полотен: полотно — в ведомости, коробка — по системе. Откос от угла помещения до проёма с коробкой — не менее 50 мм.
2. Марки в кружках — типы заполнения проёмов (ГОСТ 21.501-2018, п. 5.3.2); одна марка — один типоразмер; количество сверено с планом.
3. Открывание: Л — петли слева, П — справа, если смотреть со стороны, куда открывается полотно (на себя).
4. Скрытые двери (Д-2…Д-5): проём замерить в чистоте; блок заказать до штукатурки (≈ 30 дн.), короб ставить до штукатурки; полотно навесить после чистовой отделки, красить в цвет стен. Порядок — практика монтажа, изготовитель подтверждает.
5. Д-2…Д-4 — существующие проёмы, до техзаключения не расширять. Д-3, Д-4: стена принята 150 мм, по скану 85 мм, не замерено; узел — для 150 мм (К-25).
6. Полотно «расч.» — по проёму с запасом по каталогам, заказ — по таблице проёмов модели; Д-2…Д-5: проём 2100, а под полотно 2000 по каталогам нужен 2050–2080, под 2100 — 2150–2180: высоту проёма — по модели; Д-1: входной блок по ГОСТ 31173-2016 — задать при выборе блока.
7. Д-1: дуга наружу — по плану заказчика, не проверено; блок оставить или заменить — не решено (К-26). Окна ОК-1…ОК-4 существующие, сохраняются; подоконники и откосы не заданы — приняты (К-27).
8. Размеры проёмов и привязки сняты со скана плана заказчика и на объекте не замерены (обмерный план — лист 27).
9. Знак «*» у проёма — допущение: положение проёма не замерено (дверь пом. 5, стена В; дверь пом. 8, стена А (2 шт.)); размер напечатан как принятый; в ведомости — знак «*» в графе «Прим.». Реестр: листы 6–11, вопросы К-26, К-25.
10. Экспликация помещений — лист 27; в марках помещений — номер и площадь, м².
11. Привязка проёма к углу помещения меньше 1 мм на листе, размер на плане не показан: Д-2 — 80 мм.

Изм.	Кол.уч	Лист	№ док.	Подп.	Дата
Разраб.		Кырлан А.С.			13.11.26
Пров.					
ГИП					
Н. контр.					
Утв.					

ГД-2026-003-АИ

Трёхкомнатная квартира

Общая площадь 78,95* м² · * размеры со скана, не замерены (реестр — л. 6–11, К-13)

Дизайн-проект интерьера трёхкомнатной квартиры

Стадия	Лист	Листов
РП	30	132

План дверей и ведомость заполнения проёмов

М 1:75

Кырлан Александр Сергеевич

выпуск 13.11.2026 № 6f3a8abb2c · стр. 31 из 157

02

Планировочное решение

Кырлан Александр Сергеевич

выпуск 13.11.2026 № 6f3a8abb2c · стр. 32 из 157


Концепция интерьера

Современный (контемпорари) · схема аналоговая · 60/30/10 · материалы, образы и зонирование


Идея

Стиль — современный (контемпорари), тёплая редакция (warm contemporary): актуальность, комфорт, мягкая геометрия, контраст фактур, открытость, уверенность. Потолки V503, стены Skimming Stone No. 241, грейж H487 в текстиле, один глубокий акцент Hague Blue No. 30 (изголовья спален, ТВ-стена). Цветовая схема — аналоговая, пропорция 60/30/10: база на стенах и потолках, вторичный цвет — в текстиле и мягкой мебели, акцент — точечно.

Мудборд: материалы и фактуры

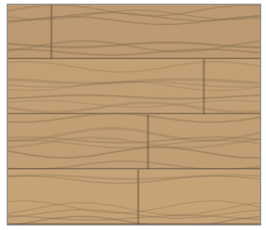

Инженерная доска, дуб натуральный
пол

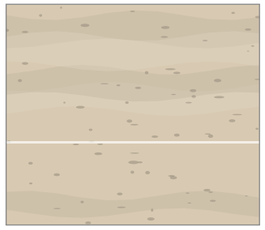

Керамогранит ректифицированный под травертин
пол



Winter · Tikkurila V503
потолок, стены, плинтус



Skimming Stone · Farrow & Ball No. 241
стены, плинтус



Hague Blue · Farrow & Ball No. 30
акцент (стена А)



Лён, Tikkurila H487
портьеры-волна, подушки декоративные на кровать

Шерсть, NCS S 3005-Y20R
ковёр под кроватью

Бархат, Farrow & Ball No. 30
подушки на кровать, подушки на диван

Букле, Farrow & Ball No. 229
подушки декоративные на кровать

Палитра 60/30/10

60 %		30 %	10 %

60 % база — Tikkurila V503 Winter, LRV 86; Farrow & Ball No. 241 Skimming Stone, LRV 67


30 % вторичный — Tikkurila H487 Pumice, LRV 57

10 % акцент — Farrow & Ball No. 30 Hague Blue, LRV 7

Свет

Цветовая температура 2700–3000 K (диапазон стиля 2700–3000 K); CRI не ниже 90; сценарии: вечер, уборка, ужин, кино, готовка. Общий свет — споты с диммированием, акцент — скрытая линейная подсветка, у кроватей — бра.

Функциональное зонирование (М 1:200)

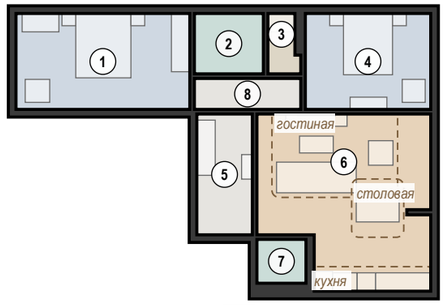

- дневная зона: гостиная, кухня, столовая
- ночная зона: спальни
- мокрая зона: санузлы
- хранение: гардеробная, кладовая
- вход и коммуникации
- функциональная зона в помещении
- (1) номер помещения (лист 32)

Образы помещений

6. Кухня-гостиная — 29,20 м²

стены Farrow & Ball No. 241; акцент No. 30 на стене А
пол — доска, дуб натуральный
текстиль: портьеры H487, тюль V503, римская штора V484, ковёр в зоне отдыха V484

1. Спальня 1 — 17,75 м²

стены Farrow & Ball No. 241; акцент No. 30 на стене А
пол — доска, дуб натуральный
текстиль: портьеры H487, тюль V503, ковёр S 3005-Y20R

4. Спальня 2 — 12,80 м²

стены Farrow & Ball No. 241; акцент No. 30 на стене А
пол — доска, дуб натуральный
текстиль: портьеры H487, тюль V503, ковёр V484
декор: картина над кроватью, зеркало в рост,

5. Прихожая — 7,13 м²

стены Farrow & Ball No. 241
пол — керамогранит под травертин, матовый
текстиль: ковёр-дорожка шерстяной безворсовый 700×2000 V484
декор: зеркало, графика в тонкой

8. Коридор — 3,50 м²

стены Farrow & Ball No. 241
пол — доска, дуб натуральный
декор: картина в коридоре
свет 3000 K

3. Гардеробная — 1,85 м²

стены Tikkurila V503
пол — доска, дуб натуральный
свет 3000 K

2. Ванная — 4,43 м²

стены — керамогранит под травертин
пол — керамогранит под травертин, матовый
текстиль: полотенца банные махровые No. 47, полотенца для рук вафельные V503, коврик для ванной у бортика ванны H487

7. Санузел 2 — 2,29 м²

стены — керамогранит под травертин
пол — керамогранит под травертин, матовый
текстиль: полотенца для рук вафельные No. 47, полотенце банное махровое V503
декор: зеркало над умывальником, ваза-кувшин

Материалы и отделка

Инженерная доска, дуб натуральный
масло, 1-полосная, 14/4 мм
пол — пом. 1, 3, 4, 6, 8

Керамогранит ректифицированный под травертин
матовый; 600×600, 600×1200
пол — пом. 2, 5, 7

Керамогранит под травертин
матовый; 600×1200, 1200×600
стены, фартук — пом. 2, 6, 7

Farrow & Ball No. 241 Skimming Stone, LRV 67
Farrow & Ball Modern Emulsion, матовая
стены, плинтус — пом. 1, 4, 5, 6, 8

Tikkurila V503 Winter, LRV 86
Tikkurila Anti-Reflex 2, глубокоматовая
потолок, стены, плинтус — пом. 1, 2, 3, 4, 5, 6, 7, 8

Farrow & Ball No. 30 Hague Blue, LRV 7
акцентная стена
акцент (стена А) — пом. 1, 4, 6

Текстиль и металл

Лён, Tikkurila H487
портьеры-волна, подушки декоративные на кровать

Вуаль, Tikkurila V503
тюль

Шерсть, NCS S 3005-Y20R
ковёр под кроватью

Бархат, Farrow & Ball No. 30
подушки на кровать, подушки на диван

Шерсть, Farrow & Ball No. 30
плед на кровать

Чёрный матовый металл
зеркало в рост, зеркало

Лён, Farrow & Ball No. 47
полотенца банные махровые, полотенца для рук вафельные

Лён, Tikkurila V503
полотенца для рук вафельные, полотенце банное махровое

Шерсть, Tikkurila H487
коврик для ванной у бортика ванны

Шерсть, Tikkurila V484
ковёр под кроватью, ковёр-дорожка шерстяной безворсовый 700×2000

Чего избегаем

1) Смешение трёх и более металлов в одной комнате
2) Мебель из каталога всё сразу одной коллекции — теряется слоистость
3) Тренды без базы: весь интерьер на букле и арках к 2027 устареет
4) Глянцевый натяжной потолок и хромированные хай-тек детали 2000-х
5) Перегрузка акцентами разного цвета (синий + зелёный + терракота в одной комнате)
6) Холодный свет 4000 K в жилых зонах

Допущения и предложения на листе. Основа листа: размеры сняты со скана плана заказчика по размерным цепочкам, контрольный обмер на объекте не выполнялся (К-13); высота потолка 2700 мм принята: на плане заказчика не указана (К-11); толщины стен приняты: наружные 250 мм, перегородки 150 мм (на плане 85–190 мм) (К-13); разрешённая мощность 15 кВт принята по типовой квартире, технических условий нет (К-14); утолщение стены 190 × 1360 мм и элемент 1470 × 160 мм плана заказчика не определены (К-12); ниши санузла 2 закрыты перегородкой и фальш-стеной: проектное решение, на плане заказчика ниша у входа открыта (К-18); несущие стены не определены: до технического заключения все существующие стены считаются несущими (К-20); окна существующие и сохраняются; подоконная доска и глубина откосов не заданы — приняты, не замерены (К-27); подрайон климата не задан — принят не северный (жилые от 2,5 м) (К-29). См. лист открытых вопросов (лист 7, записи К-11–К-14, К-18, К-20; лист 8, записи К-27, К-29).

Примечания

1. Коды цвета — по веерам производителей (колерная карта, лист 69); перед закупкой краски — выкрас на стене объекта под дневным светом и лампами проекта.
2. Материалы — по ведомости отделки (лист 67); мебель, текстиль и декор — по спецификации (лист 33). Образцы доски, керамогранита и тканей утвердить до заказа.
3. Фактуры на листе условные, цвет передан по HEX-значениям производителей: при печати возможны отклонения, решение — только по физическому образцу.

Изм.	Кол.уч	Лист	№ док.	Подп.	Дата
Разраб.		Кырлан А.С.			13.11.26
Пров.					
ГИП					
Н. контр.					
Утв.					

ГД-2026-003-АИ

Трёхкомнатная квартира

Общая площадь 78,95* м² · * размеры со скана, не замерены (реестр — л. 6–11, К-13)

Дизайн-проект интерьера трёхкомнатной квартиры

Стадия	Лист	Листов
РП	31	132

Концепция интерьера
М б/м


Кырлан Александр Сергеевич

выпуск 13.11.2026 № 6f3a8abb2c · стр. 33 из 157

План расстановки мебели

Мебель и оборудование · размеры в мм от чистовых стен · марки — по ведомости

ПРЕДВАРИТЕЛЬНО · не для производства работ · открыто пунктов: 28 (реестр — л. 6–11)

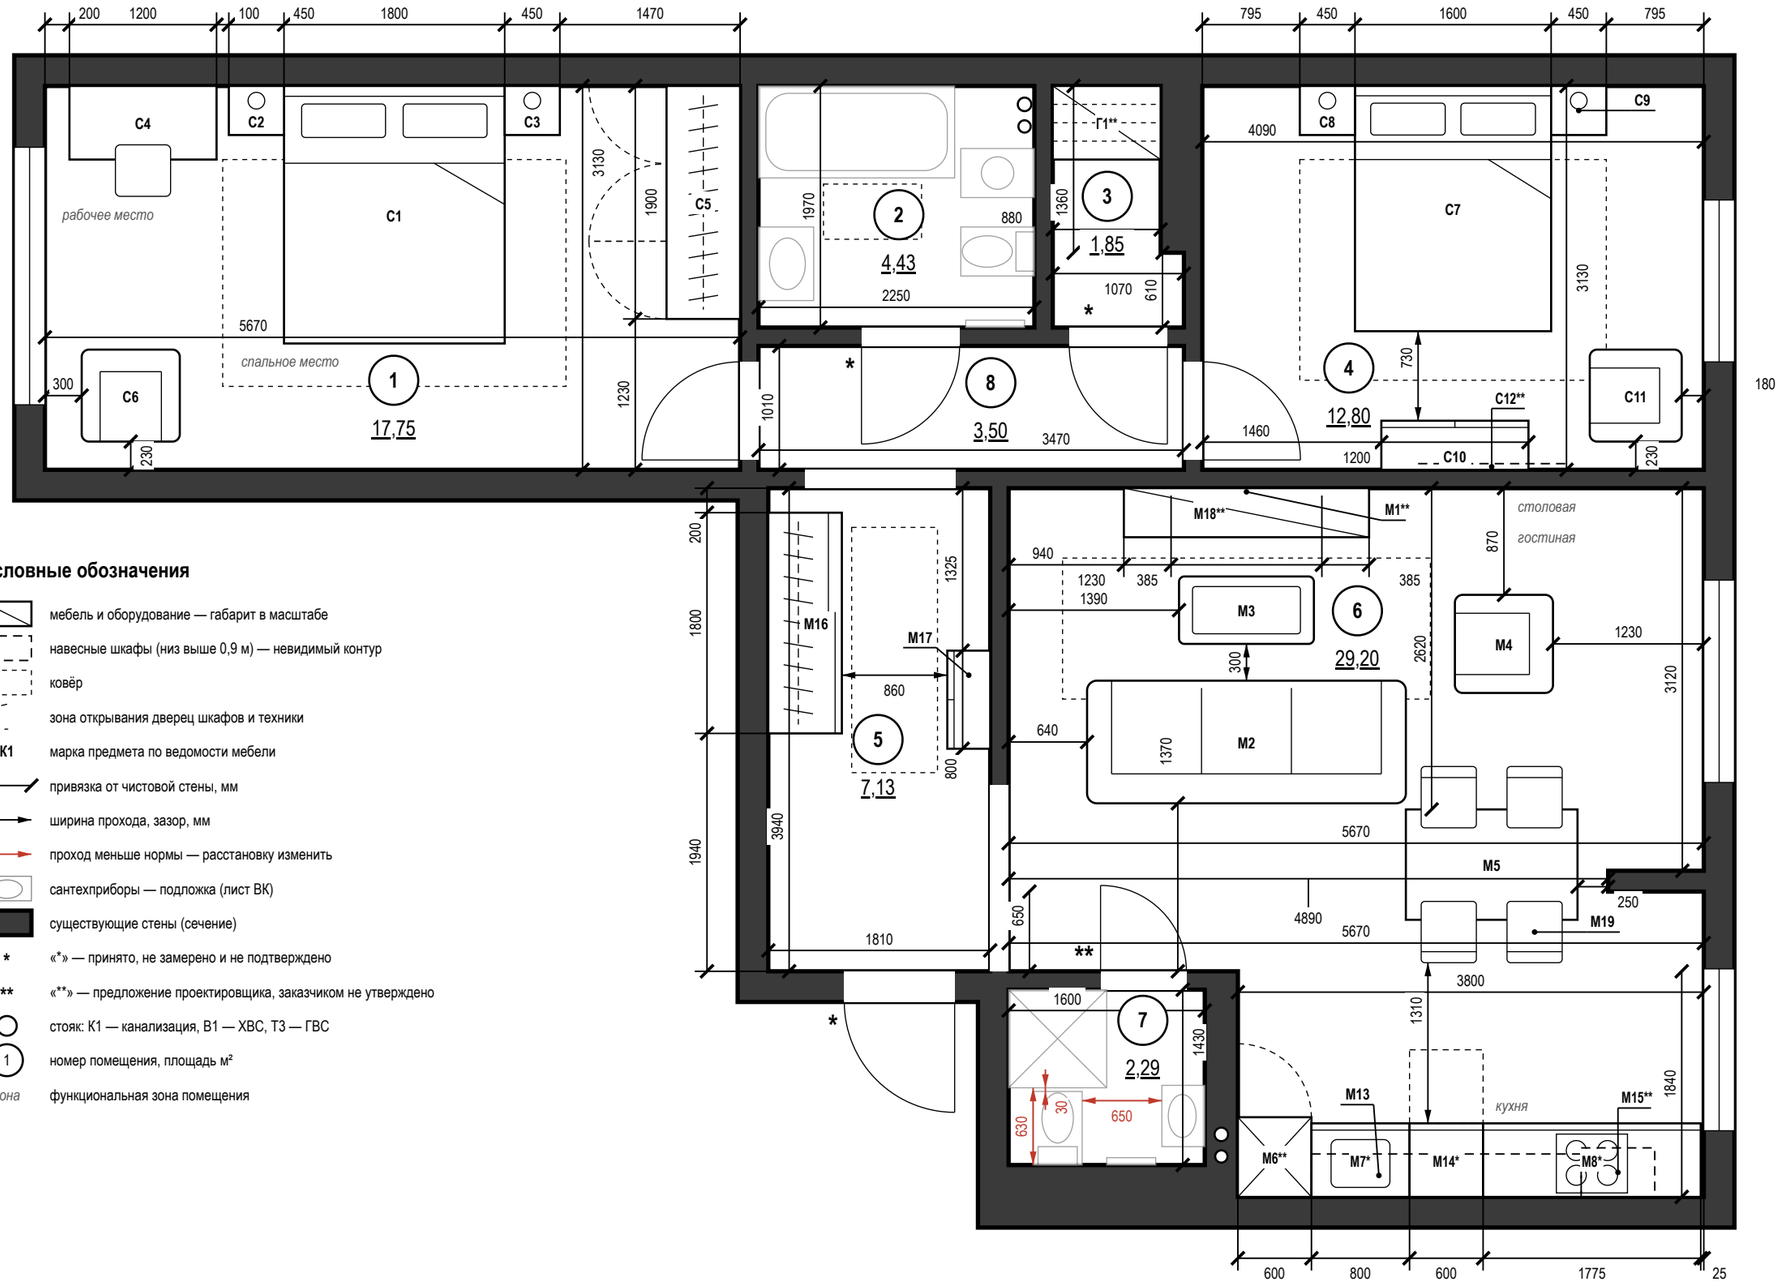

Условные обозначения

- мебель и оборудование — габарит в масштабе
- навесные шкафы (низ выше 0,9 м) — невидимый контур
- ковёр
- зона открывания дверец шкафов и техники
- **К1** — марка предмета по ведомости мебели
- привязка от чистовой стены, мм
- ширина прохода, зазор, мм
- проход меньше нормы — расстановку изменить
- сантехприборы — подложка (лист ВК)
- существующие стены (сечение)
- * — «*» — принято, не замерено и не подтверждено
- ** — «**» — предложение проектировщика, заказчиком не утверждено
- стояк: К1 — канализация, В1 — ХВС, Т3 — ГВС
- 1 — номер помещения, площадь м²
- *зона* — функциональная зона помещения

Экспликация помещений

лист 27 · на плане — номера в марках

Ведомость мебели и оборудования

Марка	Наименование	Ш×Г×В, мм	Пом.	Кол.
C1	Кровать двуспальная	1800×2100×450	1	1
C2	Тумба прикроватная	450×400×550	1	1
C3	Тумба прикроватная	450×400×550	1	1
C4	Стол письменный	1200×600×750	1	1
C5	Шкаф распашной	1900×600×2400	1	1
C6	Кресло	800×750×800	1	1
Г1**	Система хранения у торцевой стены	880×600×2400	3	1
C7	Кровать двуспальная	1600×2000×450	4	1
C8	Тумба прикроватная	450×400×550	4	1
C9	Тумба прикроватная	450×400×550	4	1
C10	Комод	1200×400×850	4	1
C11	Кресло для чтения у окна	750×750×800	4	1
C12**	ТВ 50" на кронштейне	1200×50×700	4	1
M16	Шкаф-купе	1800×600×2600	5	1
M17	Банкетка-обувница с мягким сиденьем	800×350×450	5	1
M1**	Телевизор на поворотном кронштейне	1230×60×710	6	1
M2	Диван	2600×1000×800	6	1
M3	Стол журнальный	1100×550×400	6	1
M4	Кресло	800×800×800	6	1
M5	Стол обеденный	1400×900×750	6	1
M6**	Пенал кухонный	600×650×2100	6	1
M7*	Модуль нижний с мойкой	800×600×900	6	1
M14*	Модуль под встраиваемую посудомоечную	600×600×900	6	1
M8*	Модуль нижний	1775×600×900	6	1
M13	Навесные шкафы	2200×350×720	6	1
M15**	Вытяжка над варочной панелью	600×400×570	6	1
M18**	Тумба под ТВ подвесная	2000×400×400	6	1
M19	Стул обеденный к столу M5	450×500×820	6	4

Ш — вдоль стены (изголовья), Г — от стены (длина кровати)

Материалы, модели, допуск замены — лист 33

Примечания

1. Размеры — в мм от чистовых поверхностей стен, размеры помещений — в свету, привязки — от стен, углов помещения и соседних предметов, проходы и зазоры — стрелками; розетки и выводы под мебель — лист 37, выключатели — лист 39, сантехприборы лист 48.
2. Общие указания к расстановке (чистовой слой, контрольный обмер, зазоры встроенной мебели, замена покупной) — примечания к спецификации, лист 33.
3. Стулья обеденной группы (M19 — 4 шт.) показаны в рабочем положении, задвинутыми под столешницу на 150 мм.

Допущения и предложения на листе. Знак «*» принято (замерить): Ст К1-1, Ст В1-1, Ст К1-2, Ст В1-2. Знак «**» предложено (согласовать). См. лист открытых вопросов (листы 6–11).

1000 мм · печать 1:1

Изм.	Кол.уч	Лист	№ док.	Подп.	Дата
Разраб.		Кырлан А.С.			13.11.26
Пров.					
ГИП					
Н. контр.					
Утв.					

ГД-2026-003-АИ

Трёхкомнатная квартира

Общая площадь 78,95* м² · * размеры со скана, не замерены (реестр — л. 6–11, К-13)

Дизайн-проект интерьера трёхкомнатной квартиры

Стадия	Лист	Листов
РП	32	132

План расстановки мебели

М 1:50

Кырлан Александр Сергеевич

выпуск 13.11.2026 № 6f3a8abb2c · стр. 34 из 157

Спецификация мебели и оборудования

ПРЕДВАРИТЕЛЬНО · не для производства работ · открыто пунктов: 28 (реестр — л. 6–11)

Форма 1 ГОСТ 21.110-2013 · позиции мебели — по плану расстановки

Поз.	Наименование и техническая характеристика	Тип, марка, обозначение документа, опросного листа	Код продукции	Поставщик	Ед. измерения	Кол.	Масса 1 ед., кг	Примечание
	Мебель встроенная и корпусная (изготовление по чертежам мебельщика)							
С5	Шкаф распашной; корпус ЛДСП 16 мм; фасады — МДФ 18 мм, эмаль матовая; цвет фасадов — в цвет стен (Farrow & Ball No. 241); Ш×Г×В 1900×600×2400 мм	—	—	изготовление на заказ	шт.	1	—	пом. 1; крепление к стене
Г1**	Система хранения у торцевой стены: штанга вдоль стены, полки, ящики; каркас и полки — ЛДСП 16 мм, декор «дуб натуральный»; без фасадов; Ш×Г×В 880×600×2400 мм	—	—	изготовление на заказ	шт.	1	—	пом. 3; крепление к стене
М16	Шкаф-купе; корпус ЛДСП 16 мм; фасады — ЛДСП 10 мм в алюминиевом профиле; Ш×Г×В 1800×600×2600 мм	—	—	изготовление на заказ	шт.	1	—	пом. 5
М6**	Пенал кухонный, холодильник; корпус ЛДСП 16 мм; фасады — МДФ 18 мм, эмаль матовая; цвет фасадов — в цвет стен (Farrow & Ball No. 241); Ш×Г×В 600×650×2100 мм	—	—	изготовление на заказ	шт.	1	—	пом. 6; крепление к стене
М7*	Модуль нижний с мойкой; корпус ЛДСП 16 мм; фасады — МДФ 18 мм, эмаль матовая; цвет фасадов — в цвет стен (Farrow & Ball No. 241); Ш×Г×В 800×600×900 мм	—	—	изготовление на заказ	шт.	1	—	пом. 6
М8*	Модуль нижний: ящики, варочная панель, духовой шкаф, бутылочница; корпус ЛДСП 16 мм; фасады — МДФ 18 мм, эмаль матовая; цвет фасадов — в цвет стен (Farrow & Ball No. 241); Ш×Г×В 1775×600×900 мм	—	—	изготовление на заказ	шт.	1	—	пом. 6
М13	Навесные шкафы, 3 секции; корпус ЛДСП 16 мм; фасады — МДФ 18 мм, эмаль матовая; цвет фасадов — в цвет стен (Farrow & Ball No. 241); Ш×Г×В 2200×350×720 мм	—	—	изготовление на заказ	шт.	1	—	пом. 6
М14*	Модуль под встраиваемую ПММ 60; без корпуса (ниша между соседними модулями); фасад на дверь машины — МДФ 18 мм, эмаль матовая; цоколь; цвет фасадов — в цвет стен (Farrow & Ball No. 241); Ш×Г×В 600×600×900 мм	—	—	изготовление на заказ	шт.	1	—	пом. 6
М15**	Вытяжка над варочной панелью; корпус ЛДСП 16 мм; фасады — МДФ 18 мм, эмаль матовая; цвет фасадов — в цвет стен (Farrow & Ball No. 241); Ш×Г×В 600×400×570 мм	—	—	изготовление на заказ	шт.	1	—	пом. 6
	Мебель покупная							
С1	Кровать двуспальная; мягкое изголовье, обивка — ткань, цвет Tikkurila H487; Ш×Г×В 1800×2100×450 мм	аналог: Ш×Г×В 1800×2100×450 мм, мягкое изголовье	—	аналог по характеристикам	шт.	1	—	пом. 1; замена ≤ габарита
С2, С3, С8, С9	Тумба прикроватная; шпон, дуб натуральный, матовое масло; Ш×Г×В 450×400×550 мм	аналог: Ш×Г×В 450×400×550 мм, шпон	—	аналог по характеристикам	шт.	4	—	пом. 1, 4; замена ≤ габарита
С4	Стол письменный; шпон, дуб натуральный, матовое масло; Ш×Г×В 1200×600×750 мм	аналог: Ш×Г×В 1200×600×750 мм, шпон	—	аналог по характеристикам	шт.	1	—	пом. 1; замена ≤ габарита
С6	Кресло; обивка — ткань, цвет Tikkurila H487; Ш×Г×В 800×750×800 мм	аналог: Ш×Г×В 800×750×800 мм, обивка — ткань	—	аналог по характеристикам	шт.	1	—	пом. 1; замена ≤ габарита
С7	Кровать двуспальная; мягкое изголовье, обивка — ткань, цвет Tikkurila H487; Ш×Г×В 1600×2000×450 мм	аналог: Ш×Г×В 1600×2000×450 мм, мягкое изголовье	—	аналог по характеристикам	шт.	1	—	пом. 4; замена ≤ габарита
С10	Комод; шпон, дуб натуральный, матовое масло; Ш×Г×В 1200×400×850 мм	аналог: Ш×Г×В 1200×400×850 мм, шпон	—	аналог по характеристикам	шт.	1	—	пом. 4; крепление к стене; замена ≤ габарита
С11	Кресло для чтения у окна; обивка — ткань, цвет Tikkurila H487; Ш×Г×В 750×750×800 мм	аналог: Ш×Г×В 750×750×800 мм, обивка — ткань	—	аналог по характеристикам	шт.	1	—	пом. 4; замена ≤ габарита
С12**	ТВ 50" на кронштейне над комодом С10; шпон, дуб натуральный, матовое масло; Ш×Г×В 1200×50×700 мм	аналог: Ш×Г×В 1200×50×700 мм, шпон	—	аналог по характеристикам	шт.	1	—	пом. 4; замена ≤ габарита
М17	Банкетка-обувница с мягким сиденьем, над ней настенная вешалка с полкой (низ 1650); шпон, дуб натуральный, матовое масло; Ш×Г×В 800×350×450 мм	аналог: Ш×Г×В 800×350×450 мм, шпон	—	аналог по характеристикам	шт.	1	—	пом. 5; замена ≤ габарита
М1**	Телевизор на поворотном кронштейне, центр экрана на 1150 мм от пола; диагональ 55"; крепление — настенный кронштейн по паспорту модели; Ш×Г×В 1230×60×710 мм	аналог: Ш×Г×В 1230×60×710 мм, диагональ 55"	—	аналог по характеристикам	шт.	1	—	пом. 6; замена ≤ габарита
М2	Диван; обивка — ткань, цвет Tikkurila H487; Ш×Г×В 2600×1000×800 мм	аналог: Ш×Г×В 2600×1000×800 мм, обивка — ткань	—	аналог по характеристикам	шт.	1	—	пом. 6; замена ≤ габарита

Примечания

1. Позиции мебели совпадают с марками на плане расстановки (лист 32); размеры Ш×Г×В — Ш вдоль стены, Г от стены.
2. Размеры и привязки плана расстановки — в мм от чистовых поверхностей стен: слой штукатурки 20 мм по блоку и 5 мм шпаклёвки по ГКЛ учтён; привязки — от стен и углов помещения, а не от другой мебели.
3. План расстановки не является документацией для изготовления мебели. Встроенная и корпусная мебель изготавливается по чертежам мебельщика после контрольного обмера (после штукатурки); «стена в стену» — с зазором 10 мм с каждой стороны или с компенсаторами; графы «Тип, марка» и «Код продукции» для неё не заполняются (ГОСТ 21.110-2013).
4. Покупные изделия — аналог по характеристикам: заменять только на изделия не больше указанного габарита и того же материала и цвета.
5. Материал и цвет, не указанные в данных изделия, приняты по концепции (лист 31): тон дерева — по полу, обивка — по вторичному цвету палитры; образцы согласовать до заказа.
6. Масса 1 ед. для изделий до 25 кг не указывается. Техника — по монтажным схемам изготовителя; выводы — по листам ЭОМ и ВК.

Допущения и предложения на листе. Основа листа: размеры сняты со скана плана заказчика по размерным цепочкам, контрольный обмер на объекте не выполнялся (К-13); высота потолка 2700 мм принята: на плане заказчика не указана (К-11); толщины стен приняты: наружные 250 мм, перегородки 150 мм (на плане 85–190 мм) (К-13); разрешённая мощность 15 кВт принята по типовой квартире, технических условий нет (К-14); утолщение стены 190 × 1360 мм и элемент 1470 × 160 мм плана заказчика не определены (К-12); ниши санузла 2 закрыты перегородкой и фальш-стеной: проектное решение, на плане заказчика ниша у входа открыта (К-18); несущие стены не определены: до технического заключения все существующие стены считаются несущими (К-20); окна существующие и сохраняются; подоконная доска и глубина откосов не заданы — приняты, не замерены (К-27); подрайон климата не задан — принят не северный (жилые от 2,5 м) (К-29). Знак «*» — принято, не замерено (замерить): К-8: М8. Знак «**» — предложено, не утверждено (согласовать): ИЗ-6: М1; К-7: С12; К-9: Г1. См. лист открытых вопросов (лист 6, записи К-7–К-9; лист 7, записи К-11–К-14, К-18, К-20; лист 8, записи К-27, К-29; лист 9, записи ИЗ-5, ИЗ-6).

Изм.	Кол.уч	Лист	№ док.	Подп.	Дата

Разраб.	Кырлан А.С.		13.11.26
Пров.			
ГИП			
Н. контр.			
Утв.			

ГД-2026-003-АИ

Трёхкомнатная квартира

Общая площадь 78,95* м² · * размеры со скана, не замерены (реестр — л. 6–11, К-13)

Дизайн-проект интерьера трёхкомнатной квартиры

Стадия	Лист	Листов
РП	33	132

Спецификация мебели и оборудования

М б/м

Кырлан Александр Сергеевич

выпуск 13.11.2026 № 6f3a8abb2c · стр. 35 из 157

Спецификация мебели и оборудования (продолжение)

Форма 1 ГОСТ 21.110-2013 · позиции мебели — по плану расстановки

ПРЕДВАРИТЕЛЬНО · не для производства работ · открыто пунктов: 28 (реестр — л. 6–11)

Поз.	Наименование и техническая характеристика	Тип, марка, обозначение документа, опросного листа	Код продукции	Поставщик	Ед. измерения	Кол.	Масса 1 ед., кг	Примечание
М3	Стол журнальный; шпон, дуб натуральный, матовое масло; Ш×Г×В 1100×550×400 мм	аналог: Ш×Г×В 1100×550×400 мм, шпон	—	аналог по характеристикам	шт.	1	—	пом. 6; замена ≤ габарита
М4	Кресло; обивка — ткань, цвет Tikkurila H487; Ш×Г×В 800×800×800 мм	аналог: Ш×Г×В 800×800×800 мм, обивка — ткань	—	аналог по характеристикам	шт.	1	—	пом. 6; замена ≤ габарита
М5	Стол обеденный; шпон, дуб натуральный, матовое масло; Ш×Г×В 1400×900×750 мм	аналог: Ш×Г×В 1400×900×750 мм, шпон	—	аналог по характеристикам	шт.	1	—	пом. 6; замена ≤ габарита
М18**	Тумба под ТВ подвесная, низ на 300 мм от пола; шпон, дуб натуральный, матовое масло; Ш×Г×В 2000×400×400 мм	аналог: Ш×Г×В 2000×400×400 мм, шпон	—	аналог по характеристикам	шт.	1	—	пом. 6; крепление к стене; замена ≤ габарита
М19	Стул обеденный к столу М5; обивка — ткань, цвет Tikkurila H487; каркас — дуб натуральный; Ш×Г×В 450×500×820 мм	аналог: Ш×Г×В 450×500×820 мм, обивка — ткань	—	аналог по характеристикам	шт.	4	—	пом. 6; замена ≤ габарита
	Техника встраиваемая и бытовая (покупные изделия), светильники под розетки							
	Стиральная машина, место по листу ВК (П4*); Ш×Г 400×600 мм	аналог по характеристикам: вертикальная загрузка, в плане 400 × 600 мм (ширина × глубина), по листу ВК	—	по выбору заказчика до изготовления мебели	шт.	1	—	пом. 2; по схеме изготовителя
	Холодильник встраиваемый, в модуле М6**	аналог по характеристикам: полновстраиваемый под фасад, ниша 1780 × 560 × 550 мм, вентиляция решётка в цоколе, выход сверху	—	по выбору заказчика до изготовления мебели	шт.	1	—	пом. 6; по схеме изготовителя
	Посудомоечная машина встраиваемая, в модуле М14*; ниша 600 мм	аналог по характеристикам: полновстраиваемая 60 см под фасад, ниша 600 × 862 мм, навеска фасада в комплекте	—	по выбору заказчика до изготовления мебели	шт.	1	—	пом. 6; по схеме изготовителя
	Вытяжка, в модуле М15**	аналог по характеристикам: производительность — по расчёту ОВ, шум ≤ 55 дБ(А)	—	по выбору заказчика до изготовления мебели	шт.	1	—	пом. 6; по схеме изготовителя
	Варочная панель встраиваемая, индукционная, в модуле М8*	аналог по характеристикам: индукционная 60 см, вырез 560 × 490 мм по шаблону модели	—	по выбору заказчика до изготовления мебели	шт.	1	—	пом. 6; по схеме изготовителя
	Духовой шкаф встраиваемый, в модуле М8*	аналог по характеристикам: 60 см, лицевая панель 595 мм, ниша 560 × 600, глубина ≥ 550 мм, вентиляция за прибором	—	по выбору заказчика до изготовления мебели	шт.	1	—	пом. 6; по схеме изготовителя
	Торшер, у поз. С6; абажур — ткань или опаловое стекло; лампа 2700 K	—	—	аналог по характеристикам	шт.	1	—	пом. 1; розетка Р5 (ЭОМ)
	Торшер, у поз. М18**; абажур — ткань или опаловое стекло; лампа 2700 K	—	—	аналог по характеристикам	шт.	1	—	пом. 6; розетка Р21 (ЭОМ)
	Текстиль							
Т1	Портьеры-волна; лён 100 %; цвет Tikkurila H487; карниз 2500 мм, высота 2610 мм, сборка 2	—	—	аналог по характеристикам	шт.	2	—	пом. 1
Т2	Тюль; полиэстер 100 %; цвет Tikkurila V503; карниз 2500 мм, высота 2610 мм, сборка 2,5	—	—	аналог по характеристикам	шт.	1	—	пом. 1
Т3	Ковёр под кроватью; шерсть 80 %, хлопок 20 %; цвет NCS S 3005-Y20R; 2800×1850 мм	—	—	аналог по характеристикам	шт.	1	—	пом. 1; с подложкой
Т4	Подушки декоративные на кровать; лён 100 %; цвет Tikkurila H487	—	—	аналог по характеристикам	шт.	2	—	пом. 1
Т5	Подушки на кровать, акцент; хлопковый бархат 100 %; цвет Farrow & Ball No. 30	—	—	аналог по характеристикам	шт.	2	—	пом. 1
Т6	Плед на кровать; шерсть мериноса 100 %; цвет Farrow & Ball No. 30	—	—	аналог по характеристикам	шт.	1	—	пом. 1
Т20**	Полотенца банные махровые, дымчатый зелёный, сложены на полотенцесушителе; хлопок 100 %; цвет Farrow & Ball No. 47	—	—	аналог по характеристикам	шт.	2	—	пом. 2

Допущения и предложения на листе

Основа листа: размеры сняты со скана плана заказчика по размерным цепочкам, контрольный обмер на объекте не выполнялся (К-13); высота потолка 2700 мм принята: на плане заказчика не указана (К-11); толщины стен приняты: наружные 250 мм, перегородки 150 мм (на плане 85–190 мм) (К-13); разрешённая мощность 15 кВт принята по типовой квартире, технических условий нет (К-14); утолщение стены 190 × 1360 мм и элемент 1470 × 160 мм плана заказчика не определены (К-12); ниши санузла 2 закрыты перегородкой и фальш-стеной: проектное решение, на плане заказчика ниша у входа открыта (К-18); несущие стены не определены: до технического заключения все существующие стены считаются несущими (К-20); окна существующие и сохраняются; подоконная доска и глубина откосов не заданы — приняты, не замерены (К-27); подрайон климата не задан — принят не северный (жилые от 2,5 м) (К-29).

Знак «*» — принято, не замерено и не подтверждено (замерить на объекте): ИЗ-11, К-19: П4 — вертикальная загрузка 400 × 600 мм — условие закупки (решение автора, ИЗ-11); модель не выбрана, габарит сверить по паспорту; К-8: М14; М8 — Ряд М6…М8 стена-в-стену: было 600+800+600+1800 = 3800 от х 9730 до черновой грани стены Б (13530); чистовая длина стены по развёртке 3770 (отделка 15/15) — гарнитур длиннее стены на 30 мм, зазора под компенсатор нет.

Знак «**» — предложение проектировщика, заказчиком не утверждено (согласовать с заказчиком): ИЗ-5, К-8: М6, М15; ИЗ-20: Т20; М18 — тумба под ТВ отдельно от экрана М1 (прежде один предмет «ТВ-тумба с экраном»): подвес 300 мм, верх 700 мм — ниже розеток ТВ-зоны на 1100.

См. лист открытых вопросов (лист 6, запись К-8; лист 7, записи К-11–К-14, К-18–К-20; лист 8, записи К-27, К-29; лист 9, запись ИЗ-5; лист 10, запись ИЗ-11; лист 11, запись ИЗ-20).

Изм.	Кол.уч	Лист	№ док.	Подп.	Дата
Разраб.		Кырлан А.С.			13.11.26
Пров.					
ГИП					
Н. контр.					
Утв.					

ГД-2026-003-АИ

Трёхкомнатная квартира

Общая площадь 78,95* м² · * размеры со скана, не замерены (реестр — л. 6–11, К-13)

Дизайн-проект интерьера трёхкомнатной квартиры

Стадия	Лист	Листов
РП	34	132

Спецификация мебели и оборудования (продолжение)

М б/м

Кырлан Александр Сергеевич

выпуск 13.11.2026 № 6f3a8abb2c · стр. 36 из 157

Спецификация мебели и оборудования (продолжение)

Форма 1 ГОСТ 21.110-2013 · позиции мебели — по плану расстановки

Поз.	Наименование и техническая характеристика	Тип, марка, обозначение документа, опросного листа	Код продукции	Поставщик	Ед. измерения	Кол.	Масса 1 ед., кг	Примечание
Т21**	Полотенца для рук вафельные, белые, на нижних перекладинах сушителя; хлопок 100 %; цвет Tikkurila V503	—	—	аналог по характеристикам	шт.	2	—	пом. 2
Т22**	Ковёр — коврик для ванной у бортика ванны, хлопок тафтинг, грейж; хлопок 100 %, латексная противоскользящая основа; цвет Tikkurila H487; 800×450 мм	—	—	аналог по характеристикам	шт.	1	—	пом. 2; с подложкой
Т7	Портьеры-волна; лён 100 %; цвет Tikkurila H487; карниз 1820 мм, высота 2610 мм, сборка 2	—	—	аналог по характеристикам	шт.	2	—	пом. 4
Т8	Тюль; полиэстер 100 %; цвет Tikkurila V503; карниз 1820 мм, высота 2610 мм, сборка 2,5	—	—	аналог по характеристикам	шт.	1	—	пом. 4
Т9	Ковёр под кроватью; шерсть 100 %; цвет Tikkurila V484; 2500×1800 мм	—	—	аналог по характеристикам	шт.	1	—	пом. 4; с подложкой
Т10	Подушки декоративные на кровать; букле (шерсть 60 %, полиэстер 40 %); цвет Farrow & Ball No. 229	—	—	аналог по характеристикам	шт.	2	—	пом. 4
Т11	Подушки на кровать, акцент; хлопковый бархат 100 %; цвет Farrow & Ball No. 47	—	—	аналог по характеристикам	шт.	2	—	пом. 4
Т12	Плед на кровать; шерсть мериноса 100 %; цвет Farrow & Ball No. 30	—	—	аналог по характеристикам	шт.	1	—	пом. 4
Т25**	Ковёр-дорожка шерстяной безворсовый 700×2000, серо-бежевый; шерсть 100 %; цвет Tikkurila V484; 700×2000 мм	—	—	аналог по характеристикам	шт.	1	—	пом. 5; с подложкой
Т13	Портьеры-волна (гостиная); лён 70 %, вискоза 30 %; цвет Tikkurila H487; карниз 2250 мм, высота 2610 мм, сборка 2	—	—	аналог по характеристикам	шт.	2	—	пом. 6
Т14	Тюль (гостиная); полиэстер 100 %; цвет Tikkurila V503; карниз 2250 мм, высота 2610 мм, сборка 2,5	—	—	аналог по характеристикам	шт.	1	—	пом. 6
Т15	Римская штора (кухня); лён 100 %; цвет Tikkurila V484; карниз 1400 мм, высота 1620 мм	—	—	аналог по характеристикам	шт.	1	—	пом. 6
Т16	Ковёр в зоне отдыха; шерсть 100 %; цвет Tikkurila V484; 3000×1150 мм	—	—	аналог по характеристикам	шт.	1	—	пом. 6; с подложкой
Т17	Подушки на диван; букле (шерсть 60 %, полиэстер 40 %); цвет Tikkurila H487	—	—	аналог по характеристикам	шт.	2	—	пом. 6
Т18	Подушки на диван, акцент; хлопковый бархат 100 %; цвет Farrow & Ball No. 30	—	—	аналог по характеристикам	шт.	2	—	пом. 6
Т19	Плед на диван; альпака 50 %, шерсть 50 %; цвет Tikkurila V484	—	—	аналог по характеристикам	шт.	1	—	пом. 6
Т23**	Полотенца для рук вафельные, дымчатый зелёный, на полотенцесушителе; хлопок 100 %; цвет Farrow & Ball No. 47	—	—	аналог по характеристикам	шт.	2	—	пом. 7
Т24**	Полотенце банное махровое, белое, сложено на сушителе; хлопок 100 %; цвет Tikkurila V503	—	—	аналог по характеристикам	шт.	1	—	пом. 7
	Декор							
ДК1	Картина над кроватью: абстракция, холст, тонкая рама из дуба; 1200×700 мм; низ на 1300 мм от пола	—	—	аналог по характеристикам	шт.	1	4	пом. 1; крепление к стене
ДК15**	Зеркало в рост в тонкой чёрной раме 600×1600; рама — чёрный матовый; 600×1600 мм; низ на 300 мм от пола	—	—	аналог по характеристикам	шт.	1	12	пом. 1; крепление: анкер для пустотелых оснований, 4 шт.
ДК16**	Сансевиерия в напольном керамическом кашпо Ø350, тёплый серый; 400×400 мм	—	—	аналог по характеристикам	шт.	1	—	пом. 1
ДК17**	Книги стопкой и свеча в керамической чаше на тумбе С2; 280×140 мм; на С2	—	—	аналог по характеристикам	шт.	1	—	пом. 1
ДК18**	Лампа настольная на столе С4: основание — керамика матовая, тёплый серый, абажур — лён; 220×480 мм; на С4	—	—	аналог по характеристикам	шт.	1	—	пом. 1
ДК2	Зеркало над умывальником, влагостойкое; 600×750 мм; низ на 1100 мм от пола	—	—	аналог по характеристикам	шт.	1	4	пом. 2; крепление к стене
ДК10**	Ваза-бутыль глазурованная, дымчатый зелёный, с сухой веткой эвкалипта — на полке короба инсталляции; 130×450 мм	—	—	аналог по характеристикам	шт.	1	—	пом. 2
ДК11**	Свеча в янтарном стекле и аромадиффузор с ротанговыми палочками на подносе — на полке короба; 140×200 мм	—	—	аналог по характеристикам	шт.	1	—	пом. 2

Допущения и предложения на листе

Основа листа: размеры сняты со скана плана заказчика по размерным цепочкам, контрольный обмер на объекте не выполнялся (К-13); высота потолка 2700 мм принята: на плане заказчика не указана (К-11); толщины стен приняты: наружные 250 мм, перегородки 150 мм (на плане 85–190 мм) (К-13); разрешённая мощность 15 кВт принята по типовой квартире, технических условий нет (К-14); утолщение стены 190 × 1360 мм и элемент 1470 × 160 мм плана заказчика не определены (К-12); ниши санузла 2 закрыты перегородкой и фальш-стеной: проектное решение, на плане заказчика ниша у входа открыта (К-18); несущие стены не определены: до технического заключения все существующие стены считаются несущими (К-20); окна существующие и сохраняются; подоконная доска и глубина откосов не заданы — приняты, не замерены (К-27); подрайон климата не задан — принят не северный (жилые от 2,5 м) (К-29).

Знак «**» — предложение проектировщика, заказчиком не утверждено (согласовать с заказчиком): ИЗ-20: ДК15, ДК16, ДК17, ДК18, Т21, Т22, ДК10, ДК11, Т25, Т23, Т24.

См. лист открытых вопросов (лист 7, записи К-11–К-14, К-18, К-20; лист 8, записи К-27, К-29; лист 11, запись ИЗ-20).

Изм.	Кол.уч	Лист	№ док.	Подп.	Дата
Разраб.		Кырлан А.С.			13.11.26
Пров.					
ГИП					
Н. контр.					
Утв.					

ГД-2026-003-АИ

Трёхкомнатная квартира

Общая площадь 78,95* м² · * размеры со скана, не замерены (реестр — л. 6–11, К-13)

	Стадия	Лист	Листов
Дизайн-проект интерьера трёхкомнатной квартиры	РП	35	132
Спецификация мебели и оборудования (продолжение) М б/м	**Кырлан Александр Сергеевич**		

Спецификация мебели и оборудования (продолжение)

Форма 1 ГОСТ 21.110-2013 · позиции мебели — по плану расстановки

Поз.	Наименование и техническая характеристика	Тип, марка, обозначение документа, опросного листа	Код продукции	Поставщик	Ед. измерения	Кол.	Масса 1 ед., кг	Примечание
ДК3	Картина над кроватью: графика в паспарту, рама — дуб; 1000×700 мм; низ на 1300 мм от пола	—	—	аналог по характеристикам	шт.	1	4	пом. 4; крепление к стене
ДК4	Зеркало в рост в тонкой чёрной раме; рама — чёрный матовый; 600×1600 мм; низ на 300 мм от пола	—	—	аналог по характеристикам	шт.	1	12	пом. 4; крепление: анкер для пустотелых оснований, 4 шт.
ДК19**	Вазы ручной работы разной высоты (280 и 180 мм), 2 шт., глазурь дымчатый зелёный, на комоде С10 слева от экрана; 220×280 мм; на С10	—	—	аналог по характеристикам	шт.	2	—	пом. 4
ДК20**	Замиокулькас в напольном керамическом кашпо Ø350, тёплый серый; 400×400 мм	—	—	аналог по характеристикам	шт.	1	—	пом. 4
ДК21**	Книги стопкой на тумбе С8; 280×120 мм; на С8	—	—	аналог по характеристикам	шт.	1	—	пом. 4
ДК5	Зеркало; рама — чёрный матовый; 800×1800 мм; низ на 550 мм от пола	—	—	аналог по характеристикам	шт.	1	18	пом. 5; крепление: анкер, 4 шт.
ДК13**	Графика в тонкой чёрной раме 350×500: силуэты сосен, тушь; рама — чёрный матовый; 350×500 мм; низ на 1250 мм от пола	—	—	аналог по характеристикам	шт.	1	2	пом. 5; крепление: дюбель с крюком, 2 точки
ДК6	Картина: крупная абстракция в тёплой гамме, холст на подрамнике; 1200×900 мм; центр на 1550 мм от пола	—	—	аналог по характеристикам	шт.	1	6	пом. 6; крепление: анкер, 2 шт.
ДК7	Растение в кашпо; 450×450 мм	—	—	аналог по характеристикам	шт.	1	—	пом. 6
ДК8	Ваза керамическая с ветками на обеденном столе; 200×350 мм; на М5	—	—	аналог по характеристикам	шт.	1	—	пом. 6
ДК22**	Книги по искусству стопкой и свеча в керамической чаше на журнальном столе; 300×150 мм; на М3	—	—	аналог по характеристикам	шт.	1	—	пом. 6
ДК23**	Ваза и чаша ручной работы, глазурь сине-зелёная, на тумбе М18** слева от экрана; 250×300 мм; на М18**	—	—	аналог по характеристикам	шт.	1	—	пом. 6
ДК24**	Картина над креслом М4: дюны на закате, пастель в паспарту, рама — дуб, 1000×700; 1000×700 мм; низ на 1250 мм от пола	—	—	аналог по характеристикам	шт.	1	4	пом. 6; крепление: дюбель с крюком, 2 точки
ДК25**	Ваза с ветками и чаша для фруктов ручной работы, глазурь тёплый серый, на столешнице кухни; 300×300 мм; на М8*	—	—	аналог по характеристикам	шт.	1	—	пом. 6
ДК9	Зеркало над умывальником, влагостойкое; 500×700 мм; низ на 1100 мм от пола	—	—	аналог по характеристикам	шт.	1	4	пом. 7; крепление к стене
ДК12**	Ваза-кувшин керамическая, тёплый серый, с сухоцветом (лагурус) — на полке короба инсталляции; 130×400 мм	—	—	аналог по характеристикам	шт.	1	—	пом. 7
ДК14**	Картина в коридоре: морской берег в пасмурный день, акварель в паспарту, рама — дуб, 800×600; 800×600 мм; низ на 1200 мм от пола	—	—	аналог по характеристикам	шт.	1	3	пом. 8; крепление: дюбель с крюком, 2 точки

Допущения и предложения на листе

Основа листа: размеры сняты со скана плана заказчика по размерным цепочкам, контрольный обмер на объекте не выполнялся (К-13); высота потолка 2700 мм принята: на плане заказчика не указана (К-11); толщины стен приняты: наружные 250 мм, перегородки 150 мм (на плане 85–190 мм) (К-13); разрешённая мощность 15 кВт принята по типовой квартире, технических условий нет (К-14); утолщение стены 190 × 1360 мм и элемент 1470 × 160 мм плана заказчика не определены (К-12); ниши санузла 2 закрыты перегородкой и фальш-стеной: проектное решение, на плане заказчика ниша у входа открыта (К-18); несущие стены не определены: до технического заключения все существующие стены считаются несущими (К-20); окна существующие и сохраняются; подоконная доска и глубина откосов не заданы — приняты, не замерены (К-27); подрайон климата не задан — принят не северный (жилые от 2,5 м) (К-29).

Знак «*» — принято, не замерено и не подтверждено (замерить на объекте): К-8: М8 — Ряд М6…М8 стена-в-стену: было 600+800+600+1800 = 3800 от х 9730 до черновой грани стены Б (13530); чистовая длина стены по развёртке 3770 (отделка 15/15) — гарнитур длиннее стены на 30 мм, зазора под компенсатор нет.

Знак «**» — предложение проектировщика, заказчиком не утверждено (согласовать с заказчиком): ИЗ-20: ДК19, ДК20, ДК21, ДК13, ДК22, ДК23, ДК24, ДК25, ДК12, ДК14; М18 — тумба под ТВ отдельно от экрана М1 (прежде один предмет «ТВ-тумба с экраном»): подвес 300 мм, верх 700 мм — ниже розеток ТВ-зоны на 1100.

См. лист открытых вопросов (лист 6, запись К-8; лист 7, записи К-11–К-14, К-18, К-20; лист 8, записи К-27, К-29; лист 11, запись ИЗ-20).

Изм.	Кол.уч	Лист	№ док.	Подп.	Дата
Разраб.		Кырлан А.С.			13.11.26
Пров.					
ГИП					
Н. контр.					
Утв.					

ГД-2026-003-АИ

Трёхкомнатная квартира

Общая площадь 78,95* м² · * размеры со скана, не замерены (реестр — л. 6–11, К-13)

Дизайн-проект интерьера трёхкомнатной квартиры	Стадия	Лист	Листов
	РП	36	132
Спецификация мебели и оборудования (продолжение) М б/м	**Кырлан Александр Сергеевич**		

03

Электрооборудование


Кырлан Александр Сергеевич

выпуск 13.11.2026 · 6f3a8abb2c · стр. 39 из 157

План розеток и электровыводов

Розетки, выводы кабеля, щит · размеры в мм · высоты от чистого пола

План розеток (М 1:50)

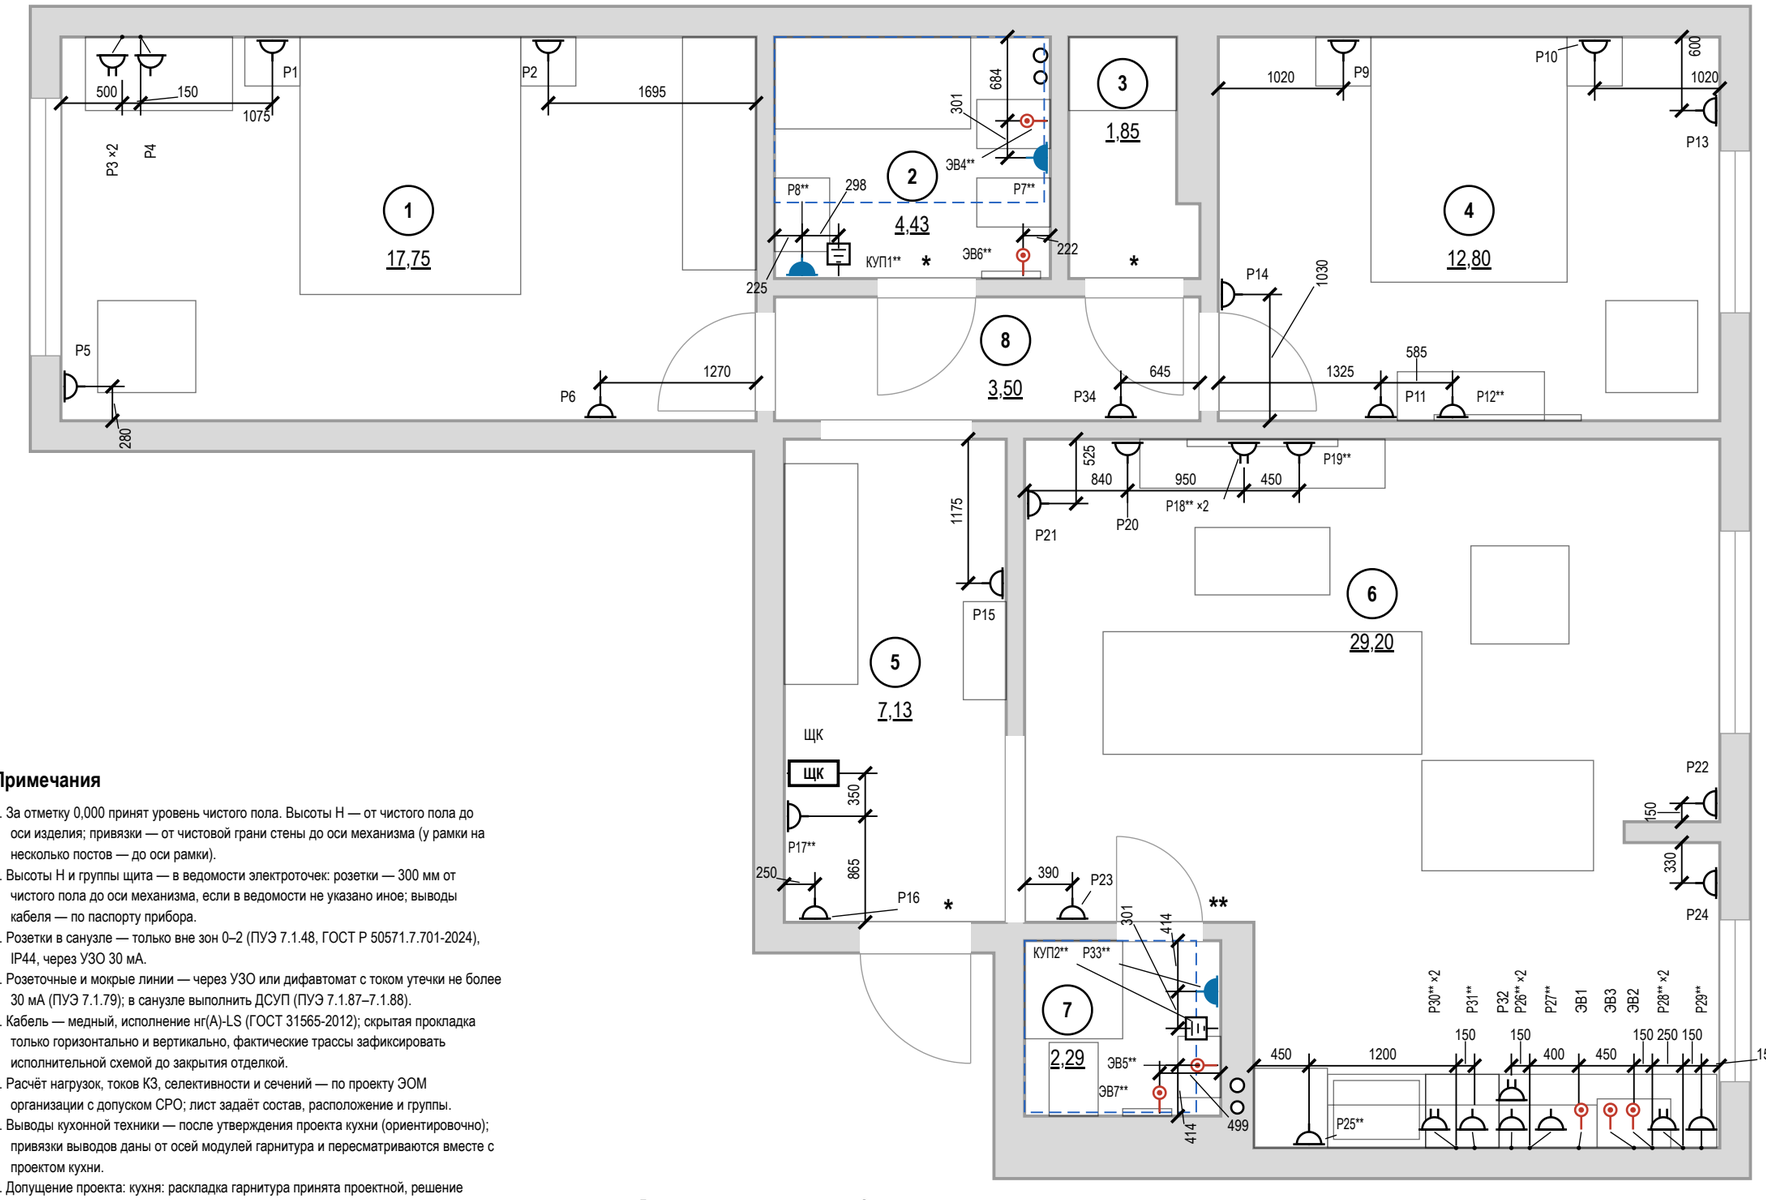

Условные обозначения

Знак	Тип изделия	Н, мм	Кол., шт
	Розетка с заземлением	300	14
	То же	у знака	12
	Блок розеток с заземлением, рамка 2 поста	у знака	5
	Розетка с заземлением IP44	1000	3
	Вывод кабеля к прибору	у знака	7
	КУП (уравнивание потенциалов)	300	2
ЩК	Щит квартирный	1700	1

розетка с заземляющим контактом; у знака — марка и ×N — число постов в рамке; группа щита, высота оси и назначение — в ведомости точек

знак разведён для читаемости: точка на стене — у выноски, привязка — до неё

граница зоны 2 ванной (600 мм от ванны/поддона)

мебель и сантехприборы — подложка

стояк: К1 — канализация, В1 — ХВС, Т3 — ГВС

1 — номер помещения, площадь м²

Итого розеток (механизмов) — 39 шт; рамок — 34 шт: на 1 пост — 29, на 2 поста — 5.

Примечания

1. За отметку 0,000 принят уровень чистого пола. Высоты Н — от чистого пола до оси изделия; привязки — от чистовой грани стены до оси механизма (у рамки на несколько постов — до оси рамки).
2. Высоты Н и группы щита — в ведомости электроточек: розетки — 300 мм от чистого пола до оси механизма, если в ведомости не указано иное; выводы кабеля — по паспорту прибора.
3. Розетки в санузле — только вне зон 0–2 (ПУЭ 7.1.48, ГОСТ Р 50571.7.701-2024), IP44, через УЗО 30 мА.
4. Розеточные и мокрые линии — через УЗО или дифавтомат с током утечки не более 30 мА (ПУЭ 7.1.79); в санузле выполнить ДСУП (ПУЭ 7.1.87–7.1.88).
5. Кабель — медный, исполнение нг(А)-LS (ГОСТ 31565-2012); скрытая прокладка только горизонтально и вертикально, фактические трассы зафиксировать исполнительной схемой до закрытия отделкой.
6. Расчёт нагрузок, токов КЗ, селективности и сечений — по проекту ЭОМ организации с допуском СРО; лист задаёт состав, расположение и группы.
7. Выводы кухонной техники — после утверждения проекта кухни (ориентировочно); привязки выводов даны от осей модулей гарнитура и пересматриваются вместе с проектом кухни.
8. Допущение проекта: кухня: раскладка гарнитура принята проектной, решение автора (ИЗ-12) — мойка М7* у шахты Ш2, ПММ М14* рядом с мойкой, варочная и духовой шкаф в М8*, вытяжка М15**, холодильник М6**; выводы техники — по типовой расстановке; условие: до начала черновых работ сверить раскладку и выводы с чертежом кухни от изготовителя, выводы пересматриваются по его чертежу (вопрос К-8).
9. Допущение проекта: стиральная машина П4* — вертикальной загрузки, габарит в плане 400 × 600 мм (ширина 400 вдоль стены Б): условие закупки, а не пожелание, решение автора (ИЗ-11); машина с фронтальной загрузкой или большего габарита не подходит — перед люком ванна П1; модель не выбрана, габарит и подводку сверить по паспорту до закрытия трасс (вопрос К-19).
10. Марки из допущений, которых нет на этом листе: М6**, М7*, М8*, М14*, М15** — лист 77; Ш2 — лист 48; П1, П4* — лист 48.
11. Электрический тёплый пол проектом не предусмотрен; при решении заказчика устроить — отдельный лист «План тёплых полов»: контуры с отступом 100 мм от стен и мебели без ножек, датчик в гофре, терморегулятор, своя группа щита через УЗО 30 мА.
12. Ведомости электроточек, изделий, светильников и расшифровка клавиш — лист 40.

1000 мм · печать 1:1

Допущения и предложения на листе. Основа листа: размеры сняты со скана плана заказчика по размерным цепочкам, контрольный обмер на объекте не выполнялся (К-13); высота потолка 2700 мм принята: на плане заказчика не указана (К-11); толщины стен приняты: наружные 250 мм, перегородки 150 мм (на плане 85–190 мм) (К-13); разрешённая мощность 15 кВт принята по типовой квартире, технических условий нет (К-14); утолщение стены 190 × 1360 мм и элемент 1470 × 160 мм плана заказчика не определены (К-12); ниши санузла 2 закрыты перегородкой и фальш-стеной: проектное решение, на плане заказчика ниша у входа открыта (К-18); несущие стены не определены: до технического заключения все существующие стены считаются несущими (К-20); окна существующие и сохраняются; подоконная доска и глубина откосов не заданы — приняты, не замерены (К-27); подрайон климата не задан — принят не северный (жилые от 2,5 м) (К-29). Знак «*» — принято, не замерено (замерить): ИЗ-11, К-19: П4; К-8: М8; К-17: Ст К1-1, Ст В1-1, Ст К1-2, Ст В1-2. Знак «**» — предложено, не утверждено (согласовать): Р26, Р27, Р28, Р29, Р30, Р31; ИЗ-1: ЭВ6, ЭВ7; ИЗ-8: ЭВ4, КУП1, ЭВ5, КУП2; К-7: Р12, Р17, Р18, Р19; К-7, К-8: Р25. См. лист открытых вопросов (лист 6, записи К-1, К-7, К-8; лист 7, записи К-11–К-14, К-17–К-20; лист 8, записи К-25–К-27, К-29; лист 9, записи ИЗ-1, ИЗ-4, ИЗ-5, ИЗ-8, ИЗ-9; лист 10, записи ИЗ-11, ИЗ-15).

Изм.	Кол.уч	Лист	№ док.	Подп.	Дата
Разраб.		Кырлан А.С.			13.11.26
Пров.					
ГИП					
Н. контр.					
Утв.					

ГД-2026-003-АИ

Трёхкомнатная квартира

Общая площадь 78,95* м² · * размеры со скана, не замерены (реестр — л. 6–11, К-13)

Дизайн-проект интерьера трёхкомнатной квартиры

Стадия	Лист	Листов
РП	37	132

План розеток и электровыводов

М 1:50


Кырлан Александр Сергеевич

выпуск 13.11.2026 № 6f3a8abb2c · стр. 40 из 157

План освещения

Светильники, группы включения, извещатели · размеры в мм

План освещения (М 1:50)

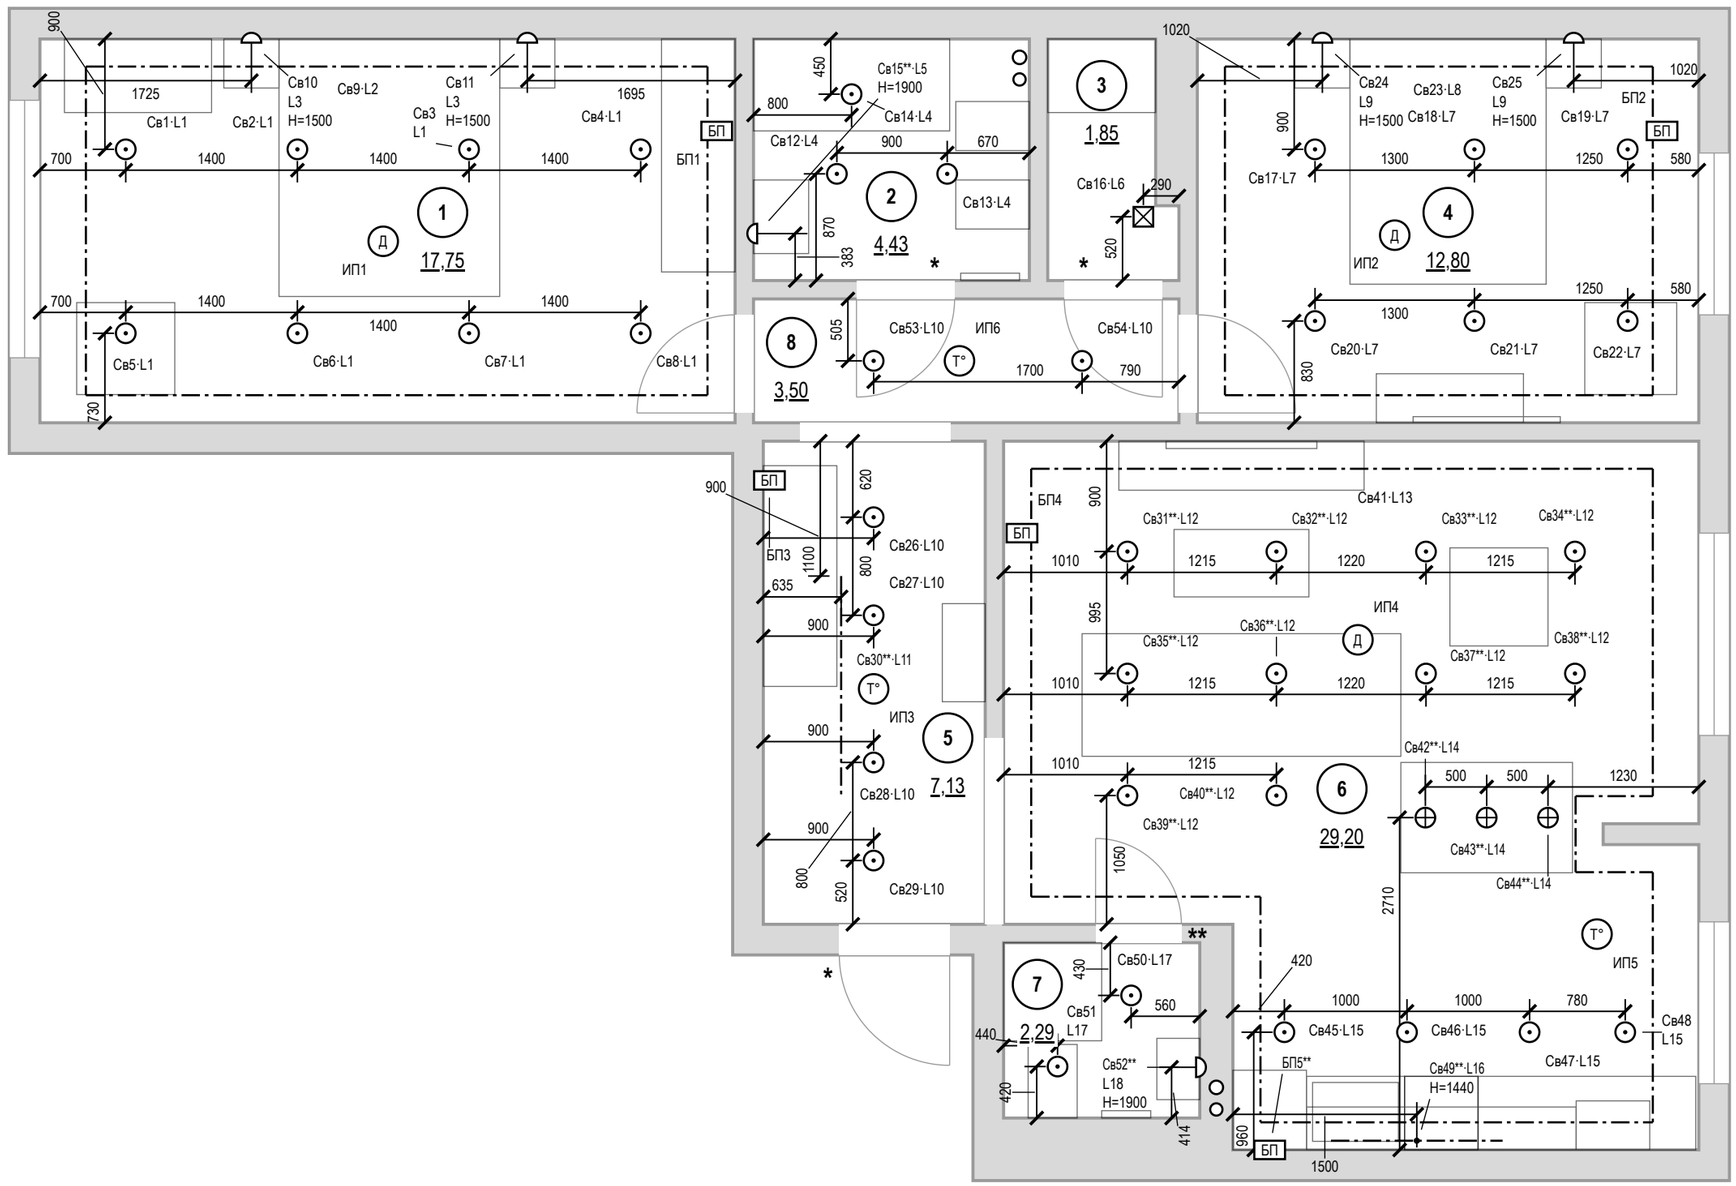

Условные обозначения

- светильник встраиваемый точечный
- светильник потолочный накладной
- светильник подвесной
- светильник настенный (бра), H — высота оси
- линейный светильник настенный (подсветка столешницы), точка — вывод питания
- светодиодная лента в профиле / в карнизе короба
- Св1·L1 — марка светильника (как в ведомости и на развёртках) · группа включения L (лист 39)
- Д — извещатель пожарный дымовой автономный
- T° — извещатель пожарный тепловой
- БП — блок питания LED, с доступом (люк от 100×100 мм)
- мебель и сантехприборы — подложка
- стояк: К1 — канализация, В1 — ХВС, Т3 — ГВС
- 1 — номер помещения, площадь м²

Допущения и предложения на листе. Основа листа: размеры сняты со скана плана заказчика по размерным цепочкам, контрольный обмер на объекте не выполнялся (К-13); высота потолка 2700 мм принята: на плане заказчика не указана (К-11); толщины стен приняты: наружные 250 мм, перегородки 150 мм (на плане 85–190 мм) (К-13); разрешённая мощность 15 кВт принята по типовой квартире, технических условий нет (К-14); утолщение стены 190 × 1360 мм и элемент 1470 × 160 мм плана заказчика не определены (К-12); ниши санузла 2 закрыты перегородкой и фальш-стеной: проектное решение, на плане заказчика ниша у входа открыта (К-18); несущие стены не определены: до технического заключения все существующие стены считаются несущими (К-20); окна существующие и сохраняются; подоконная доска и глубина откосов не заданы — приняты, не замерены (К-27); подрайон климата не задан — принят не северный (жилые от 2,5 м) (К-29). Знак «*» — принято, не замерено и не подтверждено (замерить на объекте): К-17: Ст К1-1, Ст В1-1, Ст К1-2, Ст В1-2. Знак «**» — предложение проектировщика, заказчиком не утверждено (согласовать с заказчиком): Св15 — Сдвиг под раскладку плитки стены Г на 137 мм вдоль стены — ось на шве или в центре плитки, привязка по таблице листа; Св30 — открытая лента в накладном профиле вместо «в коробе»: короба в потолке нет — подвесной потолок помещения без короба и ниши LED; Св31, Св32, Св33, Св34, Св35, Св36, Св37, Св38, Св39, Св40 — ряды — по зоне гостиной (по мебели); Св52 — Сдвиг под раскладку плитки стены Б на 14 мм вдоль стены — ось на шве или в центре плитки, привязка по таблице листа; ИЗ-3: Св42, Св43, Св44, Св49, БП5 — диммируемость добавлена разработчиком проекта под светорегуляторы S11 и S12. См. лист открытых вопросов (лист 7, записи К-11–К-14, К-17, К-18, К-20; лист 8, записи К-25–К-27, К-29; лист 9, запись ИЗ-3).

Примечания

1. За отметку 0,000 принят уровень чистого пола. Высоты H — от чистого пола до оси изделия; привязки — от чистовой грани стены до оси механизма (у рамки на несколько постов — до оси рамки).
2. Высота установки, не указанная на плане: светильники — на потолке; настенные — по отметке H у знака. Привязки — до оси светильника от чистовой грани стены, по рядам.
3. Во влажных помещениях — светильники не ниже IP44; в зонах 0–2 ванной — по ГОСТ Р 50571.7.701-2024 (зона 1 — IPX5).
4. LED-лента в карнизе подсветки короба — по линии карниза с плана потолков; блок питания — в люке короба (БП на плане), питание ленты длиннее 5 м — с двух концов.
5. Розеточные и мокрые линии — через УЗО или дифавтомат с током утечки не более 30 мА (ПУЭ 7.1.79); в санузле выполнить ДСУП (ПУЭ 7.1.87–7.1.88).
6. Кабель — медный, исполнение нг(A)-LS (ГОСТ 31565-2012); скрытая прокладка только горизонтально и вертикально, фактические трассы зафиксировать исполнительной схемой до закрытия отделкой.
7. Расчёт нагрузок, токов КЗ, селективности и сечений — по проекту ЭОМ организации с допуском СРО; лист задаёт состав, расположение и группы.
8. Ведомость светильников (тип, количество, мощность, поток, Tц, Ra) — лист 57.
9. Оценка освещённости (по норме СанПиН 1.2.3685-21, табл. 5.52, на полу; не светотехнический расчёт, декоративная подсветка в оценку не входит) — лист 40.

1000 мм · печать 1:1

Изм.	Кол.уч	Лист	№ док.	Подп.	Дата
Разраб.		Кырлан А.С.			13.11.26
Пров.					
ГИП					
Н. контр.					
Утв.					

ГД-2026-003-АИ

Трёхкомнатная квартира

Общая площадь 78,95* м² · * размеры со скана, не замерены (реестр — л. 6–11, К-13)

Дизайн-проект интерьера трёхкомнатной квартиры

Стадия	Лист	Листов
РП	38	132

План освещения

М 1:50

Кырлан Александр Сергеевич


ПРЕДВАРИТЕЛЬНО · не для производства работ · открыто пунктов: 28 (реестр — л. 6–11)

выпуск 13.11.2026 № 6f3a8abb2c · стр. 41 из 157

План выключателей и схема включения

Выключатели S, группы включения L, линии связи · размеры в мм

План выключателей (М 1:50)

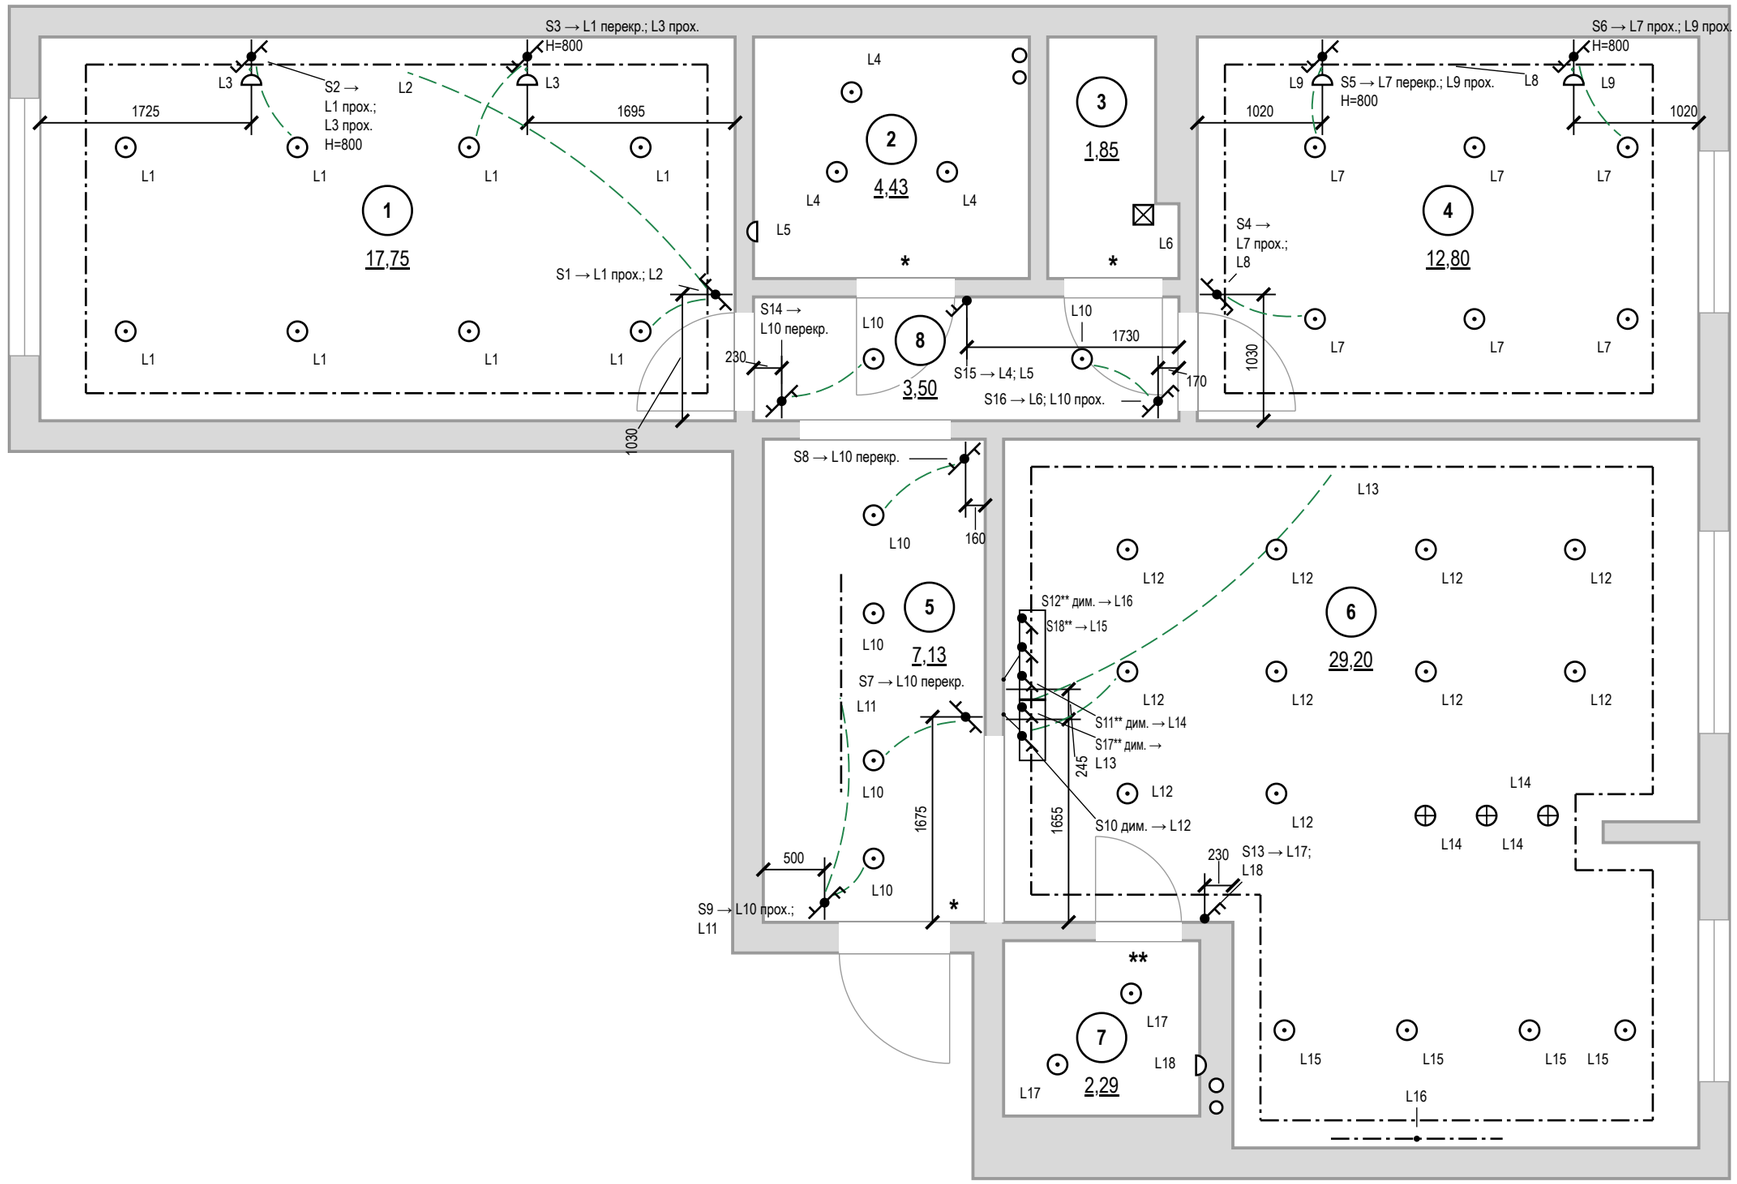

Условные обозначения

- выключатель одноклавишный
- выключатель двухклавишный (флажков — по числу клавиш)
- выключатель с проходной или перекрёстной клавишей (обратный флажок); тип клавиши — в подписи
- S1 → — марка → группы по клавишам (через «;»): прох. — проходной, перекр. — перекрёстный, дим. — светорегулятор; Н — высота
- связь: выключатель → ближайший светильник группы в том же помещении (не трасса кабеля); полный состав группы — по номеру L
- светильник встраиваемый точечный
- светильник потолочный накладной
- светильник подвесной
- светильник настенный (бра), Н — высота оси
- линейный светильник настенный (подсветка столешницы), точка — вывод питания
- светодиодная лента в профиле / в карнизе короба
- L1 — группа включения у светильника
- стояк: К1 — канализация, В1 — ХВС, Т3 — ГВС
- 1 — номер помещения, площадь м²

Допущения и предложения на листе. Основа листа: размеры сняты со скана плана заказчика по размерным цепочкам, контрольный обмер на объекте не выполнялся (К-13); высота потолка 2700 мм принята: на плане заказчика не указана (К-11); толщины стен приняты: наружные 250 мм, перегородки 150 мм (на плане 85–190 мм) (К-13); разрешённая мощность 15 кВт принята по типовой квартире, технических условий нет (К-14); утолщение стены 190 × 1360 мм и элемент 1470 × 160 мм плана заказчика не определены (К-12); ниши санузла 2 закрыты перегородкой и фальш-стеной: проектное решение, на плане заказчика ниша у входа открыта (К-18); несущие стены не определены: до технического заключения все существующие стены считаются несущими (К-20); окна существующие и сохраняются; подоконная доска и глубина откосов не заданы — приняты, не замерены (К-27); подрайон климата не задан — принят не северный (жилые от 2,5 м) (К-29). Знак «*» — принято, не замерено и не подтверждено (замерить на объекте): К-17: Ст К1-1, Ст В1-1, Ст К1-2, Ст В1-2. Знак «**» — предложение проектировщика, заказчиком не утверждено (согласовать с заказчиком): S17 — свой пост группе L13: сценарии «Вечер», «Ужин», «Кино», «Готовка» включают её отдельно от L12 — на одном светорегуляторе не набрать; S18 — свой пост группе L15: сценарии «Вечер», «Ужин», «Готовка» включают её отдельно от L14 — на одном светорегуляторе не набрать; ИЗ-3: S11, S12 — светорегулятор добавлен разработчиком проекта. См. лист открытых вопросов (лист 7, записи К-11–К-14, К-17, К-18, К-20; лист 8, записи К-25–К-27, К-29; лист 9, запись ИЗ-3).

Примечания

1. За отметку 0,000 принят уровень чистого пола. Высоты Н — от чистого пола до оси изделия; привязки — от чистовой грани стены до оси механизма (у рамки на несколько постов — до оси рамки).
2. Высота установки, не указанная на плане: выключатели — 900 мм от чистого пола (у кровати и другие — Н у марки), со стороны дверной ручки (ПУЭ 7.1.51).
3. Какой выключатель какие светильники включает — по номеру группы L: у выключателя (S1 → L1; L2 — клавиши по порядку) и у каждого светильника. Пунктир подсказка к ближайшему светильнику группы в том же помещении (не дальше 3 м), это не трасса кабеля; выключатель за стеной (у двери санузла) и далёкая группа — только номер группы.
4. Группы из нескольких мест (L1 — S1, S2, S3; L3 — S2, S3; L7 — S4, S5, S6; L9 — S5, S6; L10 — S7, S8, S9, S14, S16): на крайних местах — проходные клавиши, на промежуточных — перекрёстные; механизмы — в ведомости изделий.
5. Светорегулятор — по заднему фронту (для LED-драйверов), совместимость с драйверами проверить до закупки.
6. Розеточные и мокрые линии — через УЗО или дифавтомат с током утечки не более 30 мА (ПУЭ 7.1.79); в санузле выполнить ДСУП (ПУЭ 7.1.87–7.1.88).
7. Кабель — медный, исполнение нг(А)-LS (ГОСТ 31565-2012); скрытая прокладка только горизонтально и вертикально, фактические трассы зафиксировать исполнительной схемой до закрытия отделкой.
8. Расчёт нагрузок, токов КЗ, селективности и сечений — по проекту ЭОМ организации с допуском СРО; лист задаёт состав, расположение и группы.
9. Расшифровка клавиш и ведомость изделий — лист 40.

1000 мм · печать 1:1

Изм.	Кол.уч	Лист	№ док.	Подп.	Дата
Разраб.		Кырлан А.С.			13.11.26
Пров.					
ГИП					
Н. контр.					
Утв.					

ГД-2026-003-АИ

Трёхкомнатная квартира

Общая площадь 78,95* м² · * размеры со скана, не замерены (реестр — л. 6–11, К-13)

Дизайн-проект интерьера трёхкомнатной квартиры	Стадия	Лист	Листов
	РП	39	132
План выключателей и схема включения М 1:50	**Кырлан Александр Сергеевич**		

выпуск 13.11.2026 № 6f3a8abb2c · стр. 42 из 157

Ведомость электроточек и изделий

Электроточки, изделия, светильники, освещённость, клавиши выключателей · б/м

Ведомость электроточек

Марка	Пом.	Назначение	Н, мм	Гр.
Р1	1	у кровати	600	4
Р2	1	у кровати	600	4
Р3	1	рабочий стол	900	4
Р4	1	рабочий стол	900	4
Р5	1	торшер у кресла	300	4
Р6	1	уборка	300	4
КУП1**	2	КУП — уравнивание потенциалов (ДСУП)	300	
Р7**	2	стиральная машина, IP44	1000	12
Р8**	2	фен у умывальника, IP44	1000	13
ЭВ4**	2	вентилятор ВР1 (таймер выбега)	2403	3
ЭВ6**	2	полотенцесушитель П10**, IP44	700	13
Р9	4	у кровати	600	5
Р10	4	у кровати	600	5
Р11	4	у комода	300	5
Р12**	4	ТВ над комодом (в одной зоне с ТВ2, LAN2)	1100	5
Р13	4	уборка	300	5
Р14	4	уборка у входа	300	5
Р15	5	пылесос, сушилка обуви	300	6
Р16	5	уборка	300	6
Р17**	5	питание слаботочного щита (рядом с ЩС**)	1700	14
ЩК	5	щит квартирный ЩРВ-П-48	1700	
Р18**	6	ТВ (в одной зоне с ТВ1, LAN3) — за экраном М1** на поворотном кронштейне, доступ при отведённом экране	1100	6
Р19**	6	ТВ-приставка (в одной зоне с ТВ1, LAN3) — за экраном М1** на поворотном кронштейне, доступ при отведённом экране	1100	6
Р20	6	у ТВ-тумбы	300	6
Р21	6	торшер	300	6

Ведомость электроточек (продолжение)

Марка	Пом.	Назначение	Н, мм	Гр.
Р22	6	общего назначения	300	6
Р23	6	уборка, пылесос	300	6
Р24	6	у обеденного стола	300	6
Р25**	6	холодильник — в своём модуле, над нишей, за съёмной панелью	2000	11
Р26**	6	фартук	1175	7
Р27**	6	фартук	1175	7
Р28**	6	фартук	1200	7
Р29**	6	фартук	1200	7
Р30**	6	фартук между мойкой и варочной	1175	7
Р31**	6	фартук между мойкой и варочной	1175	7
Р32	6	посудомоечная машина	300	10
ЭВ1	6	варочная панель — за ящиком	600	8
ЭВ2	6	духовой шкаф	150	9
ЭВ3	6	вытяжка — над корпусом	2200	11
КУП2**	7	КУП — уравнивание потенциалов (ДСУП)	300	
Р33**	7	фен у умывальника, IP44	1000	13
ЭВ5**	7	вентилятор ВР3 (таймер выбега)	2343	3
ЭВ7**	7	полотенцесушитель П13**, IP44	700	13
Р34	8	уборка	300	6

Ведомость изделий

Наименование	Марки	Ед.	Кол.
Розетка с з/к и защитными шторками, 16 А	по ведомости точек	шт	36
Розетка IP44 с крышкой, 16 А	Р7**, Р8**, Р33**	шт	3
Выключатель 1-клав.	S18**	шт	1
Выключатель 1-клав. перекрёстный	S7, S8, S14	шт	3
Выключатель 2-клав.	S13, S15	шт	2
Выключатель 2-клав. (перекрёстная + проходная)	S3, S5	шт	2
Выключатель 2-клав. (проходная + обычная)	S1, S4, S9, S16	шт	4

Ведомость изделий (продолжение)

Наименование	Марки	Ед.	Кол.
Выключатель 2-клав. проходной	S2, S6	шт	2
Светорегулятор 1-канальный, задний фронт (LED)	S10, S11**, S12**, S17**	шт	4
Датчик движения ночной подсветки	L11	шт	1
Рамка 1-постовая	в т. ч. 18 под выключ.	шт	47
Рамка 2-постовая		шт	5
Коробка установочная (подрозетник) Ø68	розетки, выключатели	шт	57
Вывод кабеля под прибор (клеммник)	ЭВ1–ЭВ3, ЭВ4**, ЭВ5**, ЭВ6**, ЭВ7**	шт	7
Коробка уравнивания потенциалов КУП	КУП1**, КУП2**	шт	2
Блок питания LED 24 В, 200 Вт, дим.	БП1, БП2	шт	2
Блок питания LED 24 В, 20 Вт	БП3	шт	1
Блок питания LED 24 В, 300 Вт, дим.	БП4	шт	1
Блок питания LED 24 В, 60 Вт, дим.	БП5**	шт	1
Извещатель дымовой автономный	ИП1, ИП2, ИП4	шт	3
Извещатель тепловой	ИП3, ИП5, ИП6	шт	3
Щит квартирный (состав — лист щита)	ЩК	шт	1
Розетка компьютерная RJ45, кат. 6, с рамкой и подрозетником	LAN1–LAN3	шт	3
Розетка телевизионная (коаксиальная) с рамкой и подрозетником	ТВ1, ТВ2	шт	2
Точка доступа Wi-Fi (оборудование заказчика), питание PoE	АР1**, АР2**	шт	2
Трубка или монитор домофона (поставка домофонной организации)	ДФ1	шт	1
Щит слаботочный ЩС**: корпус, DIN-рейка, розетки 220 В	ЩС**	шт	1
Патч-панель, портов не менее 5		шт	1
Коммутатор, портов не менее 5, из них PoE 2		шт	1

Ведомость изделий (продолжение)

Наименование	Марки	Ед.	Кол.
Кабель домофона — тип по системе поставщика (по лучам от ЩС**, запас 10 %)		м	2,9
Кабель коаксиальный RG-6 (75 Ом) к розеткам ТВ (по лучам от ЩС**, запас 10 %)		м	30,3
Кабель U/UTP кат. 6 (LAN, Wi-Fi и камеры по PoE) (по лучам от ЩС**, запас 10 %)		м	62,3

Ведомость светильников

Поз.	Марки	Тип	Кол.	Р, Вт	Ф, лм	IP	Тц/Ra
1	Св1–Св8	встраиваемый точечный	8	12	1000		2700/90
2	Св9	светодиодная лента, 15,5 м	1	148,8	13950		2700/90
3	Св10, Св11, Св24, Св25	настенный (бра), Н=1500	4	6	400		2700/90
4	Св12–Св14, Св51	встраиваемый точечный	4	6	500	44	3000/90
5	Св15**, Св52**	настенный (бра), Н=1900	2	8	600	44	3000/90
6	Св16	потолочный накладной	1	10	900		3000/90
7	Св17–Св22	встраиваемый точечный	6	12	1050		2700/90
8	Св23	светодиодная лента, 12,3 м	1	118,1	11070		2700/90
9	Св26–Св29, Св53, Св54	встраиваемый точечный	6	7	600		3000/90
10	Св30**	светодиодная лента, 1,8 м	1	8,6	270		2700/90
11	Св31**, Св32**, Св33**, Св34**, Св35**, Св36**, Св37**, Св38**, Св39**, Св40**	встраиваемый точечный	10	12	1000		3000/90
12	Св41	светодиодная лента, 22,1 м	1	212,2	19890		2700/90
13	Св42**, Св43**, Св44**	подвесной	3	9	800		3000/90

Примечания

1. Ведомости сведены с планов розеток, освещения и выключателей; марки, группы и высоты — те же, что у знаков на планах.
2. Механизмы, рамки и светорегуляторы — одной серии; число постов и клавиш сверено с выбранной серией. Перекрёстная клавиша — отдельный механизм серии.
3. Освещённость (оценка) — по норме СанПиН 1.2.3685-21 (табл. 5.52, на полу), не светотехнический расчёт; декоративная подсветка в оценку не входит.
4. За отметку 0,000 принят уровень чистого пола. Высоты Н — от чистого пола до оси изделия; привязки — от чистовой грани стены до оси механизма (у рамки на несколько постов — до оси рамки).
5. Розеточные и мокрые линии — через УЗО или дифавтомат с током утечки не более 30 мА (ПУЭ 7.1.79); в санузле выполнить ДСУП (ПУЭ 7.1.87–7.1.88).
6. Кабель — медный, исполнение нг(А)-LS (ГОСТ 31565-2012); скрытая прокладка только горизонтально и вертикально, фактические трассы зафиксировать исполнительной схемой до закрытия отделкой.
7. Расчёт нагрузок, токов КЗ, селективности и сечений — по проекту ЭОМ организации с допуском СРО; лист задаёт состав, расположение и группы.
8. Допущение проекта: кухня: раскладка гарнитура принята проектной, решение автора (ИЗ-12) — мойка М7* у шахты Ш2, ПММ М14* рядом с мойкой, варочная и духовой шкаф в М8*, вытяжка М15**, холодильник М6**; выводы техники — по типовой расстановке; условие: до начала черновых работ сверить раскладку и выводы с чертежом кухни от изготовителя, выводы пересматриваются по его чертежу (вопрос К-8).
9. Допущение проекта: стиральная машина П4* — вертикальной загрузки, габарит в плане 400 × 600 мм (ширина 400 вдоль стены Б): условие закупки, а не пожелание, решение автора (ИЗ-11); машина с фронтальной загрузкой или большего габарита не подходит — перед люком ванна П1; модель не выбрана, габарит и подводку сверить по паспорту до закрытия трасс (вопрос К-19).
10. Марки из допущений, которых нет на этом листе: М6**, М7*, М8*, М14*, М15** — лист 77; Ш2 — лист 48; П1, П4* — лист 48.
11. Ведомости занимают 2 листов этого наименования: таблицы, не вошедшие в поле листа, продолжены на следующем листе.

Допущения и предложения на листе. Знак «*» принято (замерить). Знак «**» предложено (согласовать). См. лист открытых вопросов (листы 6–11).

Изм.	Кол.уч	Лист	№ док.	Подп.	Дата
Разраб.		Кырлан А.С.			13.11.26
Пров.					
ГИП					
Н. контр.					
Утв.					

ГД-2026-003-АИ

Трёхкомнатная квартира

Общая площадь 78,95* м² · * размеры со скана, не замерены (реестр — л. 6–11, К-13)

	Стадия	Лист	Листов
Дизайн-проект интерьера трёхкомнатной квартиры	РП	40	132

Ведомость электроточек и изделий

М б/м

Кырлан Александр Сергеевич

выпуск 13.11.2026 № 6f3a8ab2c · стр. 43 из 157

Ведомость электроточек и изделий (продолжение)

Электроточки, изделия, светильники, освещённость, клавиши выключателей · б/м

Ведомость светильников (продолжение)

Поз.	Марки	Тип	Кол.	P, Вт	Ф, лм	IP	Тц/Ra
14	Св45–Св48	встраиваемый точечный	4	10	900		3000/90
15	Св49**	линейный светильник, H=1440	1	18	1500		3000/90
16	Св50	встраиваемый точечный	1	7	600	44	3000/90

Освещённость (оценка)

Пом.	S, м²	Ен, лк	Ф треб., лм	Ф по пр., лм
1	17,8	150	7500	8000
2	4,4	50	620	1500
3	1,9	75	390	900
4	12,8	150	5410	6300
5	7,1	50	1000	2400
6	29,2	150	12340	16000
7	2,3	50	320	1100
8	3,5	50	490	1200

Расшифровка клавиш

Марка	Пом.	H, мм	Клав.	Механизм	Группа: светильники
S1	1	900	1	проходной	L1: Св1–Св8
			2	обычный	L2: Св9
S2	1	800	1	проходной	L1: Св1–Св8
			2	проходной	L3: Св10, Св11
S3	1	800	1	перекрёстный	L1: Св1–Св8
			2	проходной	L3: Св10, Св11
S4	4	900	1	проходной	L7: Св17–Св22
			2	обычный	L8: Св23
S5	4	800	1	перекрёстный	L7: Св17–Св22
			2	проходной	L9: Св24, Св25
S6	4	800	1	проходной	L7: Св17–Св22
			2	проходной	L9: Св24, Св25
S7	5	900	1	перекрёстный	L10: Св26–Св29, Св53, Св54
S8	5	900	1	перекрёстный	L10: Св26–Св29, Св53, Св54

Расшифровка клавиш (продолжение)

Марка	Пом.	H, мм	Клав.	Механизм	Группа: светильники
S9	5	900	1	проходной	L10: Св26–Св29, Св53, Св54
			2	обычный	L11: Св30**
S10	6	900	1	светорегулятор	L12: Св31**, Св32**, Св33**, Св34**, Св35**, Св36**, Св37**, Св38**, Св39**, Св40**
S11**	6	900	1	светорегулятор	L14: Св42**, Св43**, Св44**
S12**	6	900	1	светорегулятор	L16: Св49**
S13	6	900	1	обычный	L17: Св50, Св51
			2	обычный	L18: Св52**
S14	8	900	1	перекрёстный	L10: Св26–Св29, Св53, Св54
S15	8	900	1	обычный	L4: Св12–Св14
			2	обычный	L5: Св15**
S16	8	900	1	обычный	L6: Св16
			2	проходной	L10: Св26–Св29, Св53, Св54
S17**	6	900	1	светорегулятор	L13: Св41
S18**	6	900	1	обычный	L15: Св45–Св48

Допущения и предложения на листе

Основа листа: размеры сняты со скана плана заказчика по размерным цепочкам, контрольный обмер на объекте не выполнялся (К-13); высота потолка 2700 мм принята: на плане заказчика не указана (К-11); толщины стен приняты: наружные 250 мм, перегородки 150 мм (на плане 85–190 мм) (К-13); разрешённая мощность 15 кВт принята по типовой квартире, технических условий нет (К-14); утолщение стены 190 × 1360 мм и элемент 1470 × 160 мм плана заказчика не определены (К-12); ниши санузла 2 закрыты перегородкой и фальш-стеной: проектное решение, на плане заказчика ниша у входа открыта (К-18); несущие стены не определены: до технического заключения все существующие стены считаются несущими (К-20); окна существующие и сохраняются; подоконная доска и глубина откосов не заданы — приняты, не замерены (К-27); подрайон климата не задан — принят не северный (жилые от 2,5 м) (К-29).

Знак «**» — предложение проектировщика, заказчиком не утверждено (согласовать с заказчиком): Св15 — Сдвиг под раскладку плитки стены Г на 137 мм вдоль стены — ось на шве или в центре плитки, привязка по таблице листа; Св30 — открытая лента в накладном профиле вместо «в коробе»: короба в потолке нет — подвесной потолок помещения без короба и ниши LED; S17 — свой пост группе L13: сценарии «Вечер», «Ужин», «Кино», «Готовка» включают её отдельно от L12 — на одном светорегуляторе не набрать; S18 — свой пост группе L15: сценарии «Вечер», «Ужин», «Готовка» включают её отдельно от L14 — на одном светорегуляторе не набрать; Св31, Св32, Св33, Св34, Св35, Св36, Св37, Св38, Св39, Св40 — ряды — по зоне гостиной (по мебели); Св52 — Сдвиг под раскладку плитки стены Б на 14 мм вдоль стены — ось на шве или в центре плитки, привязка по таблице листа; ИЗ-3: S11, S12 — светорегулятор добавлен разработчиком проекта; Св42, Св43, Св44, Св49 — диммируемость добавлена разработчиком проекта под светорегуляторы S11 и S12.

Открытые вопросы и конфликты по листу: К-7.

См. лист открытых вопросов (лист 6, запись К-7; лист 7, записи К-11–К-14, К-18, К-20; лист 8, записи К-27, К-29; лист 9, запись ИЗ-3).

Примечания

1. Продолжение ведомостей: лист 2 из 2 этого наименования; таблицы, прерванные на предыдущем листе, продолжены с заголовком «(продолжение)».
2. За отметку 0,000 принят уровень чистого пола. Высоты H — от чистого пола до оси изделия; привязки — от чистовой грани стены до оси механизма (у рамки на несколько постов — до оси рамки).
3. Розеточные и мокрые линии — через УЗО или дифавтомат с током утечки не более 30 мА (ПУЭ 7.1.79); в санузле выполнить ДСУП (ПУЭ 7.1.87–7.1.88).
4. Кабель — медный, исполнение нг(A)-LS (ГОСТ 31565-2012); скрытая прокладка только горизонтально и вертикально, фактические трассы зафиксировать исполнительной схемой до закрытия отделкой.
5. Расчёт нагрузок, токов КЗ, селективности и сечений — по проекту ЭОМ организации с допуском СРО; лист задаёт состав, расположение и группы.

Изм.	Кол.уч	Лист	№ док.	Подп.	Дата
Разраб.		Кырлан А.С.			13.11.26
Пров.					
ГИП					
Н. контр.					
Утв.					

ГД-2026-003-АИ

Трёхкомнатная квартира

Общая площадь 78,95* м² · * размеры со скана, не замерены (реестр — л. 6–11, К-13)

Дизайн-проект интерьера трёхкомнатной квартиры

Стадия	Лист	Листов
РП	41	132

Ведомость электроточек и изделий (продолжение)


М б/м

Кырлан Александр Сергеевич

выпуск 13.11.2026 № 6f3a8abb2c · стр. 44 из 157

Однолинейная схема щита

Щит квартирный ЩК · без масштаба

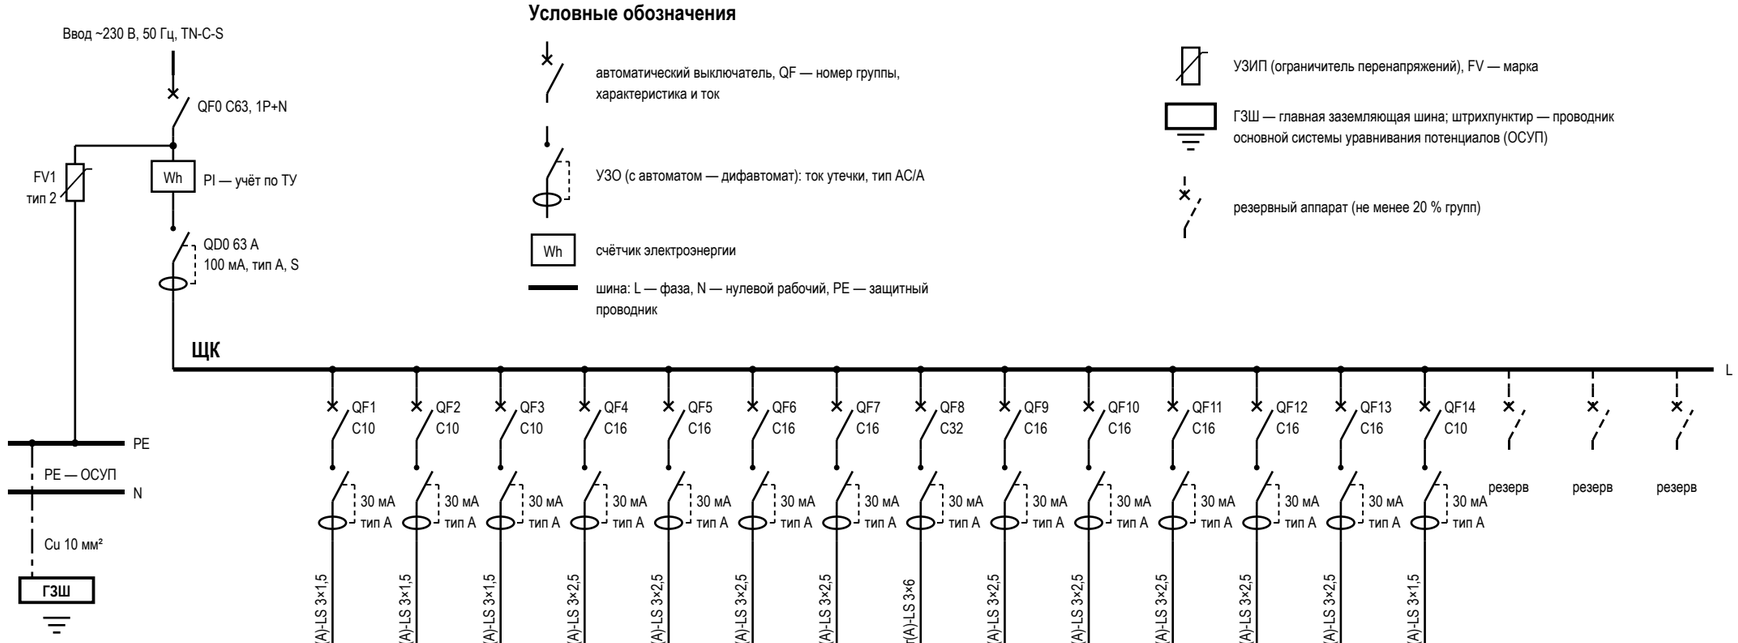

Условные обозначения

- автоматический выключатель, QF — номер группы, характеристика и ток
- УЗО (с автоматом — дифавтомат): ток утечки, тип AC/A
- Wh — счётчик электроэнергии
- шина: L — фаза, N — нулевой рабочий, PE — защитный проводник
- УЗИП (ограничитель перенапряжений), FV — марка
- ГЗШ — главная заземляющая шина; штрихпунктир — проводник основной системы уравнивания потенциалов (ОСУП)
- резервный аппарат (не менее 20 % групп)

Данные щитка

Показатель	Значение
Номер щитка	ЩК
Тип	ЩРВ-П-48, IP41
Уст. мощность, кВт	25,85
Разреш. мощность, кВт	15
Расчётная, кВт	11,8
Автоматы 1п: занят. / рез.	14 / 3
Модулей: всего / занято	48 / 34
Ток на вводе, А	63
Вводной аппарат	QF0 C63, 1P+N
УЗИП	FV1, тип 2, ЩК, после счётчика
ГЗШ, проводник ОСУП	Cu 10 мм²

Допущения и предложения на листе

Основа листа: размеры сняты со скана плана заказчика по размерным цепочкам, контрольный обмер на объекте не выполнялся (К-13); высота потолка 2700 мм принята: на плане заказчика не указана (К-11); толщины стен приняты: наружные 250 мм, перегородки 150 мм (на плане 85–190 мм) (К-13); разрешённая мощность 15 кВт принята по типовой квартире, технических условий нет (К-14); утолщение стены 190 × 1360 мм и элемент 1470 × 160 мм плана заказчика не определены (К-12); ниши санузла 2 закрыты перегородкой и фальш-стеной: проектное решение, на плане заказчика ниша у входа открыта (К-18); несущие стены не определены: до технического заключения все существующие стены считаются несущими (К-20); окна существующие и сохраняются; подоконная доска и глубина откосов не заданы — приняты, не замерены (К-27); подрайон климата не задан — принят не северный (жилые от 2,5 м) (К-29).

Открытые вопросы и конфликты по листу: К-14.

См. лист открытых вопросов (лист 7, записи К-11–К-14, К-18, К-20; лист 8, записи К-27, К-29).

Таблица групп щита ЩК и кабельный журнал

№	Назначение	Помещения	Автомат	УЗО / дифавтомат	Кабель	Длина, м	Р, кВт	Точек
1	освещение спален и гардеробной	1, 3, 4, 8	C10	30 мА, тип A	ВВГнг(A)-LS 3×1,5	94,2	0,5	30
2	освещение прихожей и кухни-гостиной	5, 6, 8	C10	30 мА, тип A	ВВГнг(A)-LS 3×1,5	91,2	0,5	38
3	освещение ванной и санузла 2	2, 6, 7, 8	C10	30 мА, тип A	ВВГнг(A)-LS 3×1,5	58,2	0,05	11
4	розетки спальни 1	1	C16	30 мА, тип A	ВВГнг(A)-LS 3×2,5	31,1	1,5	6
5	розетки спальни 2	4	C16	30 мА, тип A	ВВГнг(A)-LS 3×2,5	30,3	1,5	6
6	розетки гостиной и прихожей	5, 6, 8	C16	30 мА, тип A	ВВГнг(A)-LS 3×2,5	52,1	2	10
7	розетки фартука кухни	6	C16	30 мА, тип A	ВВГнг(A)-LS 3×2,5	28,2	2,5	6
8	варочная панель	6	C32	30 мА, тип A	ВВГнг(A)-LS 3×6	15,4	7	1
9	духовой шкаф	6	C16	30 мА, тип A	ВВГнг(A)-LS 3×2,5	15,5	3	1
10	посудомоечная машина	6	C16	30 мА, тип A	ВВГнг(A)-LS 3×2,5	14,4	2	1
11	холодильник и вытяжка	6	C16	30 мА, тип A	ВВГнг(A)-LS 3×2,5	14,2	0,6	2
12	стиральная машина	2	C16	30 мА, тип A	ВВГнг(A)-LS 3×2,5	13,2	2,2	1
13	розетки ванной и санузла 2 (фен), полотенцесушители	2, 7	C16	30 мА, тип A	ВВГнг(A)-LS 3×2,5	31,9	2,4	4
14	слаботочный щит (роутер, ONT)	5	C10	30 мА, тип A	ВВГнг(A)-LS 3×1,5	3,6	0,1	1
	Итого по сечениям ВВГнг(A)-LS, м: 3×1,5 — 247,2; 3×2,5 — 230,9; 3×6 — 15,4					493,5		

Примечания

1. Схема однолинейная: одна линия — фаза, N и PE группы; аппараты — в отключённом положении (ГОСТ 2.702, ГОСТ 2.755). Номера групп — как у точек на планах (гр.). За отметку 0,000 принят уровень чистого пола; высота щита — по плану розеток.
2. Розеточные и мокрые линии — через УЗО или дифавтомат с током утечки не более 30 мА (ПУЭ 7.1.79); в санузле выполнить ДСУП (ПУЭ 7.1.87–7.1.88).
3. УЗО тип A — для линий с электроникой, стиральной и посудомоечной машиной, LED-драйверами; тип AC — только для чисто активной нагрузки.
4. Кабель — медный, исполнение нг(A)-LS (ГОСТ 31565-2012); скрытая прокладка только горизонтально и вертикально, фактические трассы зафиксировать исполнительной схемой до закрытия отделкой.
5. Номинал автомата — не выше допустимого тока кабеля: 1,5 мм² — до 10 А, 2,5 мм² — до 16 А. Резерв щита — не менее 20 % модулей.
6. Расчёт нагрузок, токов КЗ, селективности и сечений — по проекту ЭОМ организации с допуском СРО; лист задаёт состав, расположение и группы.
7. УЗИП FV1 — после вводного автомата, проводник к шине PE — кратчайший, без петель. Шина PE щита соединяется с ГЗШ проводником ОСУП; к ГЗШ присоединяются трубы водопровода и отопления на вводе в квартиру (ПУЭ 7.1.87). Шины N и PE — раздельные, после разделения PEN не объединяются.
8. До подключения нагрузки — приёмо-сдаточные испытания с протоколом: сопротивление изоляции линий не менее 0,5 МОм, срабатывание УЗО по току и времени, непрерывность защитных проводников PE (ПУЭ, гл. 1.8).

Изм.	Кол.уч	Лист	№ док.	Подп.	Дата
Разраб.		Кырлан А.С.			13.11.26
Пров.					
ГИП					
Н. контр.					
Утв.					

ГД-2026-003-АИ

Трёхкомнатная квартира

Общая площадь 78,95* м² · * размеры со скана, не замерены (реестр — л. 6–11, К-13)

Дизайн-проект интерьера трёхкомнатной квартиры

Стадия	Лист	Листов
РП	42	132

Однолинейная схема щита

М б/м


Кырлан Александр Сергеевич

План принципиальных трасс

Силовые трассы и объёмы электромонтажа, слаботочка в объёмах · размеры в мм

План принципиальных трасс (М 1:75)

Допущения и предложения на листе. Основа листа: размеры сняты со скана плана заказчика по размерным цепочкам, контрольный обмер на объекте не выполнялся (К-13); высота потолка 2700 мм принята: на плане заказчика не указана (К-11); толщины стен приняты: наружные 250 мм, перегородки 150 мм (на плане 85–190 мм) (К-13); разрешённая мощность 15 кВт принята по типовой квартире, технических условий нет (К-14); утолщение стены 190 × 1360 мм и элемент 1470 × 160 мм плана заказчика не определены (К-12); ниши санузла 2 закрыты перегородкой и фальш-стеной: проектное решение, на плане заказчика ниша у входа открыта (К-18); несущие стены не определены: до технического заключения все существующие стены считаются несущими (К-20); окна существующие и сохраняются; подоконная доска и глубина откосов не заданы — приняты, не замерены (К-27); подрайон климата не задан — принят не северный (жилые от 2,5 м) (К-29). Знак «*» — принято, не замерено и не подтверждено (замерить на объекте): К-17: Ст К1-1, Ст В1-1, Ст К1-2, Ст В1-2. Знак «**» — предложение проектировщика, заказчиком не утверждено (согласовать с заказчиком): ИЗ-9, ИЗ-17, К-7: ЩС — щит слаботочный: место и состав. См. лист открытых вопросов (лист 6, запись К-7; лист 7, записи К-11–К-14, К-17, К-18, К-20; лист 8, записи К-25–К-27, К-29; лист 9, запись ИЗ-9; лист 11, запись ИЗ-17).

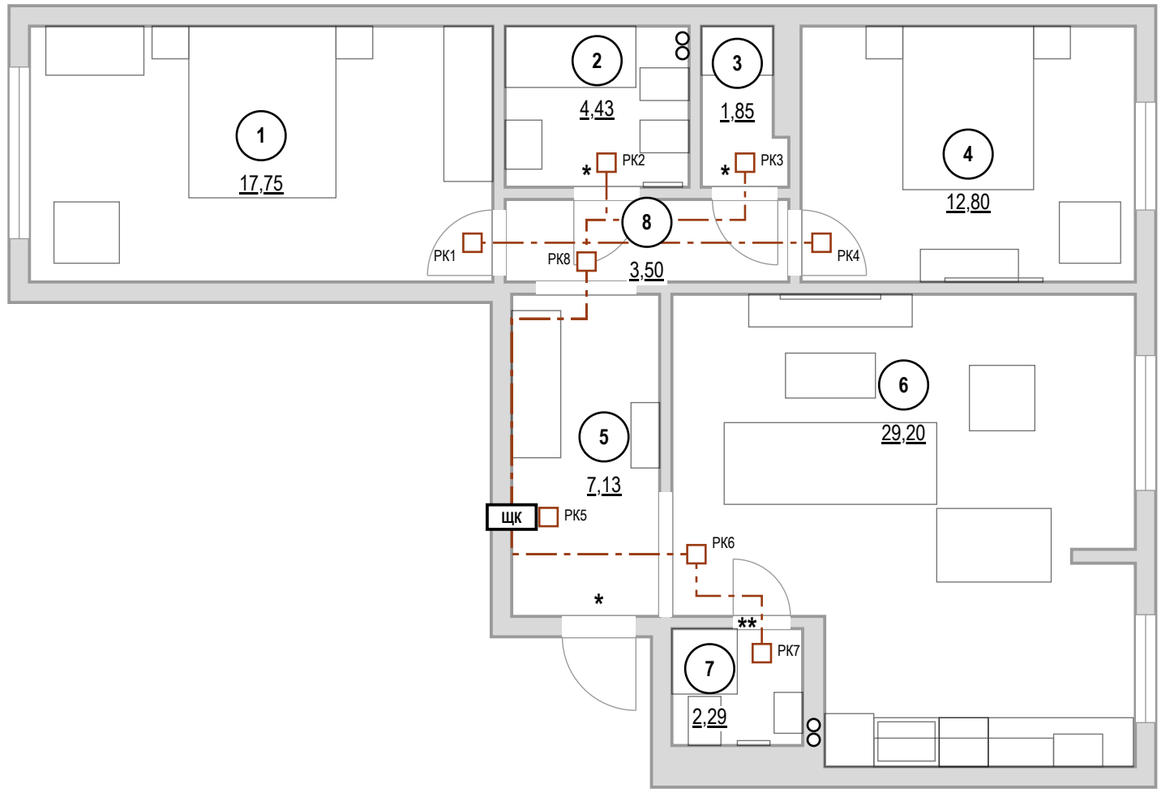

Кабель по группам ВВГнг(А)-LS, м

Гр.	мм²	Трасса	Данные
1	3×1,5	94,1	94,2
2	3×1,5	90,6	91,2
3	3×1,5	57,3	58,2
4	3×2,5	31,1	31,1
5	3×2,5	30,3	30,3
6	3×2,5	52,1	52,1
7	3×2,5	29,2	28,2

Гр.	мм²	Трасса	Данные
8	3×6	15,4	15,4
9	3×2,5	15,5	15,5
10	3×2,5	14,4	14,4
11	3×2,5	14,2	14,2
12	3×2,5	13,2	13,2
13	3×2,5	31,9	31,9
14	3×1,5	3,6	3,6
Σ		**492,9**	**493,5**

Экспликация помещений

№	Помещение	Площадь, м²
1	Спальня 1	17,75
2	Ванная	4,43
3	Гардеробная	1,85
4	Спальня 2	12,80
5	Прихожая	7,13
6	Кухня-гостиная	29,20
7	Санузел 2	2,29
8	Коридор	3,50
	Итого (общая площадь)	78,95

Объёмы прокладки

Работа, материал	Ед.	Кол.
Гофротруба Ø20 в потолочном пространстве	м	191,2
Кабель-канал плинтуса для силовых линий	м	127
Короб или накладной канал для вертикальных спусков и подъёмов	м	89,9
Коробка распределительная (РК) над дверью помещения	шт	8
Слаботочка: кабель домофона	м	2,9
Слаботочка: Кабель коаксиальный RG-6 (75 Ом) к розеткам ТВ	м	30,3
Слаботочка: U/UTP кат. 6 (LAN, Wi-Fi, камеры)	м	62,3
Слаботочка: гофротруба Ø20 отдельно от силовых	м	86

Штробы — только после заключения

Работа	Ед.	Кол.
Вертикальные штробы 20×20 мм от потолка до каждой настенной точки (в маршрут без штроб не входят)	м	105,95

Условные обозначения

- ЩК — щит квартирный
- РК — распределительная коробка над дверью помещения
- магистраль от щита к РК: потолочное пространство, гофра
- мебель и сантехприборы — подложка

Примечания

1. За отметку 0,000 принят уровень чистого пола. Высоты Н — от чистого пола до оси изделия; привязки — от чистовой грани стены до оси механизма (у рамки на несколько постов — до оси рамки).
2. Розеточные и мокрые линии — через УЗО или дифавтомат с током утечки не более 30 мА (ПУЭ 7.1.79); в санузле выполнить ДСУП (ПУЭ 7.1.87–7.1.88).
3. Кабель — медный, исполнение нг(А)-LS (ГОСТ 31565-2012); скрытая прокладка только горизонтально и вертикально, фактические трассы зафиксировать исполнительной схемой до закрытия отделкой.
4. Расчёт нагрузок, токов КЗ, селективности и сечений — по проекту ЭОМ организации с допуском СРО; лист задаёт состав, расположение и группы.
5. Длины — по плану: от щита вверх в потолочное пространство, по дверям и коридору без захода в мокрые помещения к распределительной коробке над дверью, далее к точкам; вертикали считаются вниз и обратно (у последней точки цепочки — в один конец); запас 10 %. Трассы принципиальные: фактическую зафиксировать исполнительной схемой до закрытия отделкой.
6. Несущие стены не определены: штробы в стенах не выполнять. Маршрут проложен без штроб: горизонтали — за потолком в гофре (191,2 м) и в кабель-канале плинтуса (127 м), вертикали — в коробе или накладном канале (158,3 м кабеля). Точек: за потолком — 50, спуск из потолка — 14, по плинтусу — 15, плинтус и подъём — 39.
7. Вариант со штробами — работа после технического заключения: 105,95 м вертикальных штроб от потолка до каждой настенной точки; условие — только после технического заключения: стена не несущая (или вертикальная штроба в несущей согласована конструктором), глубина и ширина 20–25 мм, не в зонах 0–2 ванной. Без заключения и согласования конструктора в смету и в график эта работа не входит.
8. В данных проекта (журнал щита) длины кабеля внесены оценкой (494 м), по трассам из геометрии — 493 м (0 %): к закупке и в смету принимать длины по трассам, а оценку в данных проекта заменить.
9. Слаботочные сети: кабели и точки считаются по лучам от ЩС** (лист слаботочных сетей): 96 м, портов патч-панели и коммутатора не менее 5; из точек 2 предложения листа слаботочки, не подтверждённые заказчиком. Изделия — в ведомости изделий.

1000 мм · печать 1:1

Изм.	Кол.уч	Лист	№ док.	Подп.	Дата
Разраб.		Кырлан А.С.			13.11.26
Пров.					
ГИП					
Н. контр.					
Утв.					

ГД-2026-003-АИ

Трёхкомнатная квартира

Общая площадь 78,95* м² · * размеры со скана, не замерены (реестр — л. 6–11, К-13)

Дизайн-проект интерьера трёхкомнатной квартиры

Стадия	Лист	Листов
РП	43	132

План принципиальных трасс

М 1:75

Кырлан Александр Сергеевич

выпуск 13.11.2026 № 6f3a8abb2c · стр. 46 из 157

Таблица нагрузок щита

щит ЩК · 14 групп · Ррасч 10,2 кВт · без масштаба

Группы щита ЩК (1)

№	Назначение	Руст, кВт	Кс	Ррасч, кВт	Iрасч, А	Автомат	Кабель
1	освещение спален и гардеробной	0,5	0,6	0,3	1,4	C10	3×1,5
2	освещение прихожей и кухни-гостиной	0,5	0,6	0,3	1,4	C10	3×1,5
3	освещение ванной и санузла 2	0,05	0,6	0,03	0,1	C10	3×1,5
4	розетки спальни 1	1,5	0,4	0,6	2,7	C16	3×2,5
5	розетки спальни 2	1,5	0,4	0,6	2,7	C16	3×2,5
6	розетки гостиной и прихожей	2	0,4	0,8	3,7	C16	3×2,5
7	розетки фартука кухни	2,5	0,4	1	4,6	C16	3×2,5

Группы щита ЩК (2)

№	Назначение	Руст, кВт	Кс	Ррасч, кВт	Iрасч, А	Автомат	Кабель
8	варочная панель	7	0,6	4,2	19,2	C32	3×6
9	духовой шкаф	3	0,6	1,8	8,2	C16	3×2,5
10	посудомоечная машина	2	0,7	1,4	6,4	C16	3×2,5
11	холодильник и вытяжка	0,6	0,4	0,24	1,1	C16	3×2,5
12	стиральная машина	2,2	0,7	1,54	7	C16	3×2,5
13	розетки ванной и санузла 2 (фен), полотенцесушители	2,4	0,7	1,68	7,7	C16	3×2,5
14	слаботочный щит (роутер, ONT)	0,1	0,4	0,04	0,2	C10	3×1,5

Итог по квартире

Показатель	Значение
Установленная мощность Σ Руст	25,85 кВт
Σ Руст × Кс по группам	14,53 кВт
Коэффициент одновременности	0,7
Расчётная мощность квартиры Ррасч	10,2 кВт
Расчётный ток Iрасч (230 В, cosφ 0,95)	47 А
Разрешённая мощность	15 кВт
Запас до разрешённой	32,2 %
Вводной аппарат	C63, 1P+N

Примечания

1. Руст — установленная мощность группы по данным щита (приборы — по паспорту, розетки общего назначения — оценка 0,1 кВт на гнездо). Кс — коэффициенты спроса: освещение 0,6; розетки 0,4; варочная и духовой 0,6; кондиционеры 0,8; тёплый пол 1,0; прочие 0,7; одновременность 0,7.
2. Коэффициенты — ориентир исполнителя, не табличные значения нормы; расчёт нагрузки подтверждает инженер ЭОМ (СП 256.1325800.2016). Под разрешённую мощность они не подгоняются.
3. Вывод: запас 32 % (расчётная 10,2 кВт при разрешённой 15 кВт).
4. Розеточные и мокрые линии — через УЗО или дифавтомат с током утечки не более 30 мА (ПУЭ 7.1.79); в санузле выполнить ДСУП (ПУЭ 7.1.87–7.1.88).

Допущения и предложения на листе

Основа листа: размеры сняты со скана плана заказчика по размерным цепочкам, контрольный обмер на объекте не выполнялся (К-13); высота потолка 2700 мм принята: на плане заказчика не указана (К-11); толщины стен приняты: наружные 250 мм, перегородки 150 мм (на плане 85–190 мм) (К-13); разрешённая мощность 15 кВт принята по типовой квартире, технических условий нет (К-14); утолщение стены 190 × 1360 мм и элемент 1470 × 160 мм плана заказчика не определены (К-12); ниши санузла 2 закрыты перегородкой и фальш-стеной: проектное решение, на плане заказчика ниша у входа открыта (К-18); несущие стены не определены: до технического заключения все существующие стены считаются несущими (К-20); окна существующие и сохраняются; подоконная доска и глубина откосов не заданы — приняты, не замерены (К-27); подрайон климата не задан — принят не северный (жилые от 2,5 м) (К-29).

См. лист открытых вопросов (лист 7, записи К-11–К-14, К-18, К-20; лист 8, записи К-27, К-29).

Изм.	Кол.уч	Лист	№ док.	Подп.	Дата
Разраб.		Кырлан А.С.			13.11.26
Пров.					
ГИП					
Н. контр.					
Утв.					

ГД-2026-003-АИ

Трёхкомнатная квартира

Общая площадь 78,95* м² · * размеры со скана, не замерены (реестр — л. 6–11, К-13)

Дизайн-проект интерьера трёхкомнатной квартиры

Стадия	Лист	Листов
РП	44	132

Таблица нагрузок щита

М б/м

Кырлан Александр Сергеевич


выпуск 13.11.2026 № 6f3a8abb2c · стр. 47 из 157

План слаботочных сетей

Интернет, ТВ, домофон · размеры в мм · высоты от чистого пола

ПРЕДВАРИТЕЛЬНО · не для производства работ · открыто пунктов: 28 (реестр — л. 6–11)

План слаботочных сетей (М 1:50)

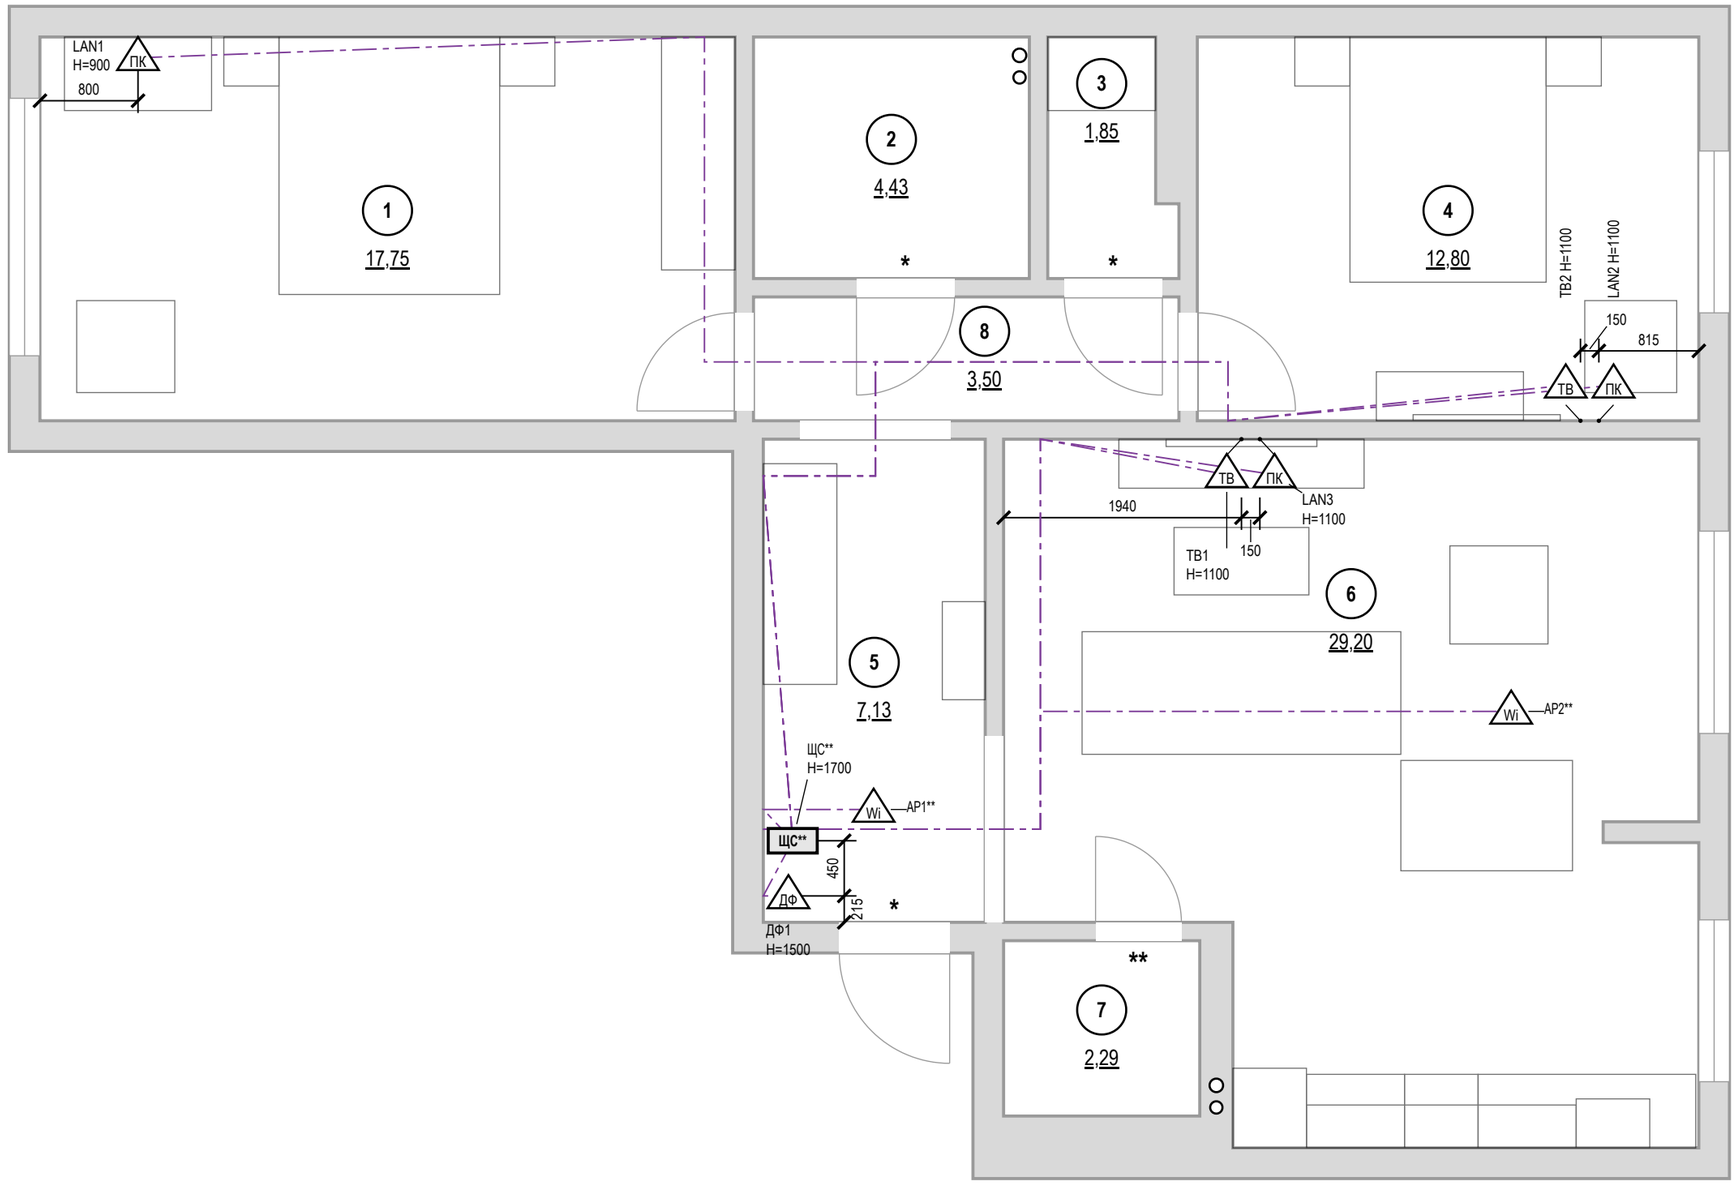

Ведомость слаботочных точек

Марка	Пом.	Назначение	Н, мм	Кабель
LAN1	1	розетка LAN (RJ45)	900	U/UTP кат. 6
TB2	4	розетка ТВ	1100	RG-6
LAN2	4	розетка LAN (RJ45)	1100	U/UTP кат. 6
ЩС**	5	щит слаботочный	1700	ввод пров.
ДФ1	5	домофон (трубка)	1500	по системе
AP1**	5	точка доступа Wi-Fi		U/UTP кат. 6
TB1	6	розетка ТВ	1100	RG-6
LAN3	6	розетка LAN (RJ45)	1100	U/UTP кат. 6
AP2**	6	точка доступа Wi-Fi		U/UTP кат. 6

Условные обозначения

- **ЩС** — щит слаботочный: ввод провайдера, роутер, коммутатор
- ПК — розетка компьютерная RJ45
- ТВ — розетка телевизионная
- ДФ — трубка или монитор домофона
- Wi — точка доступа Wi-Fi (питание PoE)
- кабель от ЩС до точки, отдельным лучом
- мебель и сантехприборы — подложка
- стояк: К1 — канализация, В1 — ХВС, Т3 — ГВС
- 1 — номер помещения, площадь м²

Допущения и предложения на листе. Основа листа: размеры сняты со скана плана заказчика по размерным цепочкам, контрольный обмер на объекте не выполнялся (К-13); высота потолка 2700 мм принята: на плане заказчика не указана (К-11); толщины стен приняты: наружные 250 мм, перегородки 150 мм (на плане 85–190 мм) (К-13); разрешённая мощность 15 кВт принята по типовой квартире, технических условий нет (К-14); утолщение стены 190 × 1360 мм и элемент 1470 × 160 мм плана заказчика не определены (К-12); ниши санузла 2 закрыты перегородкой и фальш-стеной: проектное решение, на плане заказчика ниша у входа открыта (К-18); несущие стены не определены: до технического заключения все существующие стены считаются несущими (К-20); окна существующие и сохраняются; подоконная доска и глубина откосов не заданы — приняты, не замерены (К-27); подрайон климата не задан — принят не северный (жилые от 2,5 м) (К-29). Знак «*» — принято, не замерено и не подтверждено (замерить на объекте): К-17: Ст К1-1, Ст В1-1, Ст К1-2, Ст В1-2. Знак «**» — предложение проектировщика, заказчиком не утверждено (согласовать с заказчиком): ИЗ-9, ИЗ-17, К-7: ЩС — щит слаботочный: место и состав; ИЗ-17: AP1, AP2 — точка доступа Wi-Fi: число и места. См. лист открытых вопросов (лист 6, запись К-7; лист 7, записи К-11–К-14, К-17, К-18, К-20; лист 8, записи К-25–К-27, К-29; лист 9, запись ИЗ-9; лист 11, запись ИЗ-17).

Примечания

1. За отметку 0,000 принят уровень чистого пола. Высоты Н — от чистого пола до оси изделия; привязки — от чистовой грани стены до оси механизма (у рамки на несколько постов — до оси рамки).
2. Высота установки, не указанная на плане: розетки LAN и ТВ — 300 мм от чистого пола.
3. Слаботочные кабели — отдельно от силовых: в своей трубе или лотке, при параллельной прокладке не ближе 100 мм к силовым, пересечения под прямым углом; каждую точку — отдельным кабелем от ЩС** без скруток.
4. Трассы на листе — принципиальные; фактические зафиксировать исполнительной схемой до закрытия отделкой. Силовые линии, УЗО 30 мА, ДСУП, кабель нг(А)-LS — по листам розеток и щита.
5. Проект силовой части и расчёт токов КЗ — по проекту ЭОМ; слаботочная часть согласуется с провайдером и управляющей компанией (домофон, коллективное ТВ).

1000 мм · печать 1:1

Изм.	Кол.уч	Лист	№ док.	Подп.	Дата
Разраб.		Кырлан А.С.			13.11.26
Пров.					
ГИП					
Н. контр.					
Утв.					

ГД-2026-003-АИ

Трёхкомнатная квартира

Общая площадь 78,95* м² · * размеры со скана, не замерены (реестр — л. 6–11, К-13)

Дизайн-проект интерьера трёхкомнатной квартиры

Стадия	Лист	Листов
РП	45	132

План слаботочных сетей

М 1:50

Кырлан Александр Сергеевич

выпуск 13.11.2026 № 6f3a8abb2c · стр. 48 из 157

04

Отопление и вентиляция

Кырлан Александр Сергеевич


выпуск 13.11.2026 · 6f3a8abb2c · стр. 49 из 157

План вентиляции

Вытяжка, приток, переток · кондиционирование не предусмотрено · размеры в мм · высоты от чистого пола

ПРЕДВАРИТЕЛЬНО · не для производства работ · открыто пунктов: 28 (реестр — л. 6–11)

План вентиляции (М 1:50)

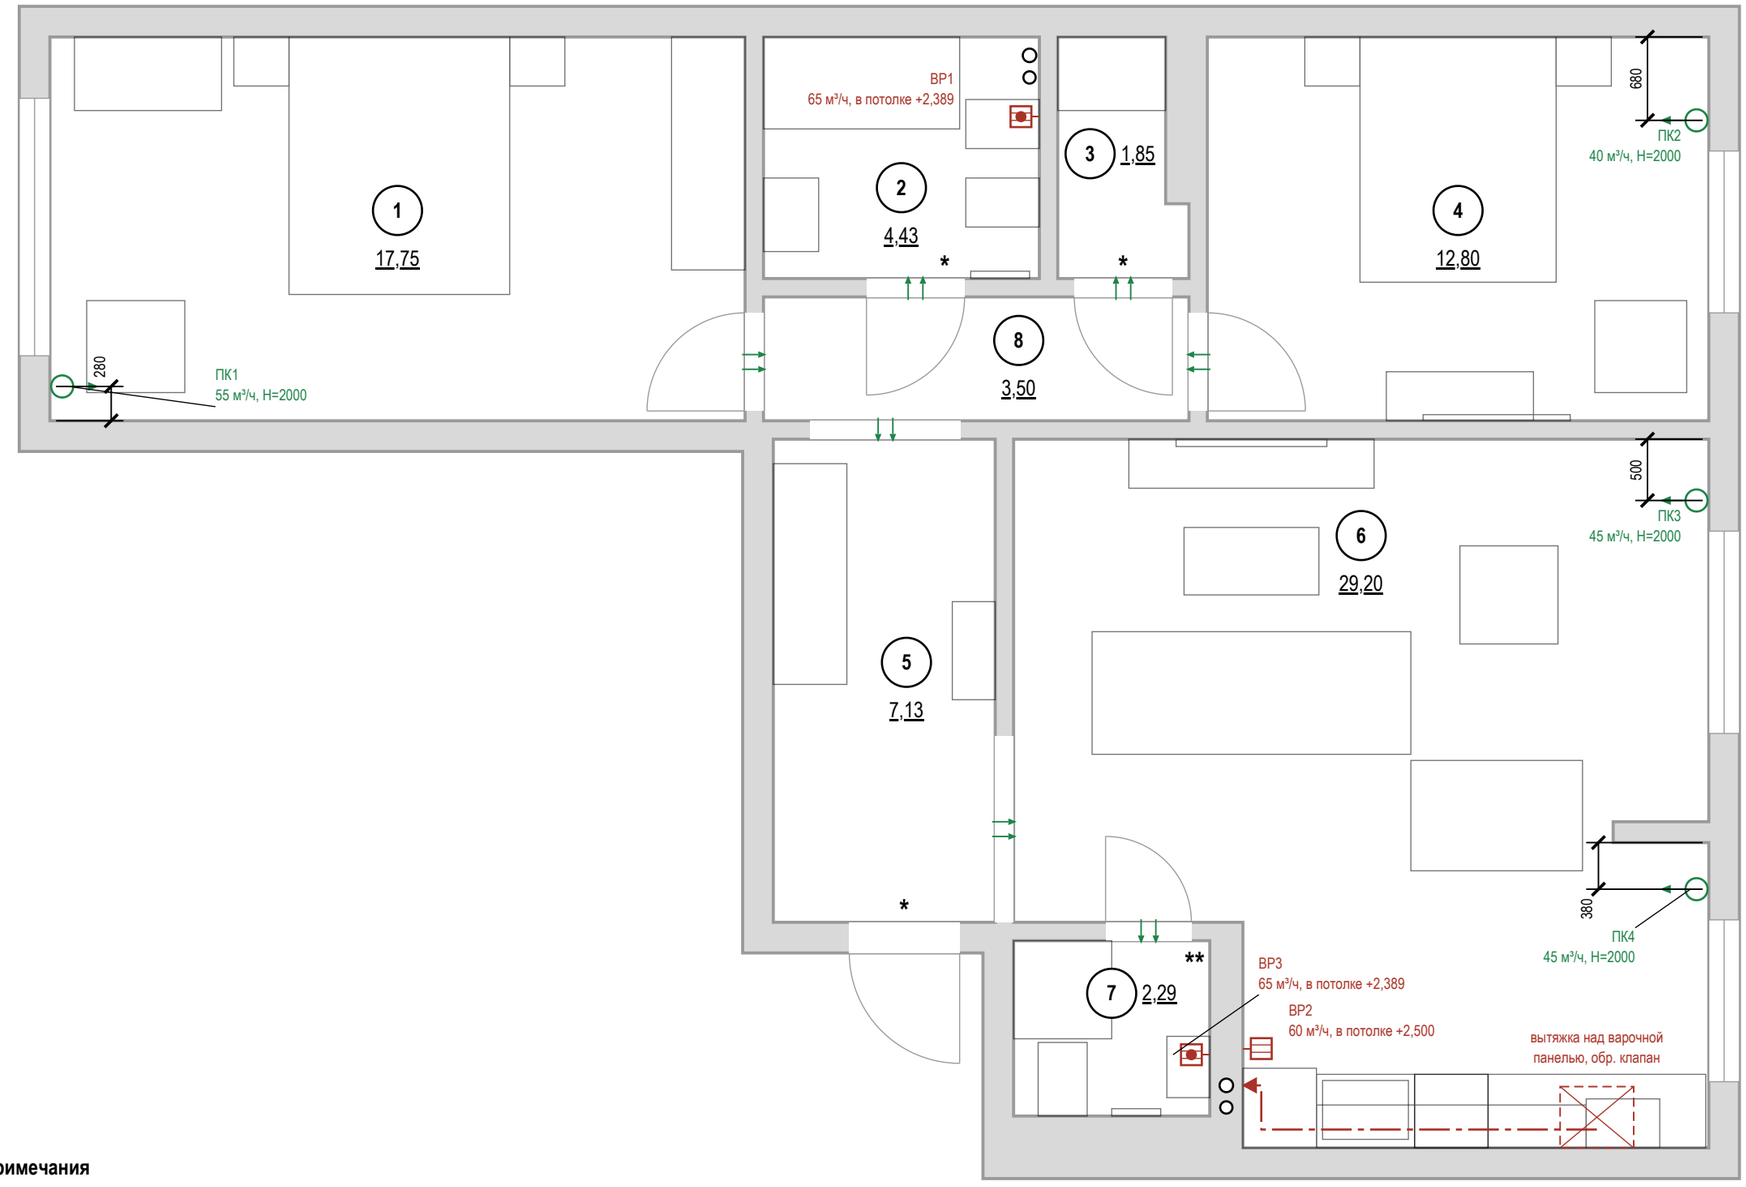

Условные обозначения

- стояк: К1 — канализация, В1 — ХВС, Т3 — ГВС
- номер помещения, площадь м²
- вытяжная решётка в подшивном потолке, воздуховод за потолком до канала
- вентилятор с обратным клапаном в подшивном потолке, воздуховод за потолком до канала
- приточный клапан (КИВ) в наружной стене: марка, расход, Н центра
- переток: зазор под полотном или переточная решётка
- кухонная вытяжка над варочной панелью
- воздуховод кухонной вытяжки в коробе под потолком
- отдельный вход воздуховода в вентканал, обратный клапан
- * — «*» — принято, не замерено и не подтверждено
- ** — «**» — предложение проектировщика, заказчиком не утверждено

Воздухообмен, м³/ч

№	Помещение	Выт. норма	Выт. проект	Прит. норма	Прит. проект	Устрой-ства
1	Спальня 1			54	55	ПК1
2	Ванная	50	65			ВР1
3	Гардеробная	1				переток
4	Спальня 2			39	40	ПК2
6	Кухня-гостиная	60	60	88	90	ВР2, ПК3, ПК4
7	Санузел 2	50	65			ВР3
	Итого	**161**	**190**	**181**	**185**	

Воздухообмен квартиры — по большей из сумм притока и вытяжки: норма 181 м³/ч, проект 190 м³/ч.
Вытяжка не меньше притока — баланс сведён.

Привязки — до обмера
Вентканалы в исходных данных не заданы: решётки и вход вытяжки показаны у стояков К1 (вентблок у мокрой зоны). До черновых работ — обмер каналов и проверка тяги; лист перевыпустить по факту.

Примечания

1. Расчёт систем ОВ и подбор оборудования — проектная организация с допуском СРО; лист даёт места, трассы и привязки.
2. Нормы вытяжки — СП 54.13330.2022 (Изм. 1, 2), табл. 7.1: кухня с электроплитой 60 м³/ч, с газовой 100; ванная и совмещённый санузел 50; уборная 25; гардеробная 0,2 ч⁻¹. Приток в жилые — 3 м³/ч на 1 м² (менее 20 м² общей площади на человека), иначе 30 м³/ч на человека.
3. Вентканалы и шахты не сужать, не переносить и не закрывать; вентилятор и кухонная вытяжка — через обратный клапан, без перекрытия естественной тяги.
4. Проектные расходы — не ниже нормы, вытяжка сведена с притоком вентиляторами мокрых помещений. Клапаны — в простенке у окна, центр 2000 мм, не над кроватью, не ближе 300 мм к стоякам отопления; типоразмер — на расход.
5. Под подшивным потолком вытяжка — в потолке, воздуховодом за потолком до канала. Кухонная вытяжка в воздухообмен не включена: воздуховод не менее Ø125 в коробе, вход в канал отдельный.
6. Переток — зазор под полотнами межкомнатных дверей или переточная решётка.
7. Кондиционирование заданием не предусмотрено; при установке трассы фреона и дренажа (не менее 40 мм/м, в К1 через сифон) и питание заложить до черновых работ.
8. Привязки оборудования — по паспортам приобретённых моделей, до черновых работ.
9. Знак «*» у проёма — допущение: положение проёма не замерено (дверь пом. 5, стена В; дверь пом. 8, стена А (2 шт.)); размер напечатан как принятый. Реестр: листы 6–11, вопросы К-26, К-25.

1000 мм · печать 1:1

Допущения и предложения на листе. Знак «*» принято (замерить): Ст К1-1, Ст В1-1, Ст К1-2, Ст В1-2. Знак «**» предложено (согласовать). См. лист открытых вопросов (листы 6–11).

Изм.	Кол.уч	Лист	№ док.	Подп.	Дата
Разраб.		Кырлан А.С.			13.11.26
Пров.					
ГИП					
Н. контр.					
Утв.					

ГД-2026-003-АИ

Трёхкомнатная квартира

Общая площадь 78,95* м² · * размеры со скана, не замерены (реестр — л. 6–11, К-13)

Дизайн-проект интерьера трёхкомнатной квартиры

Стадия	Лист	Листов
РП	46	132

План вентиляции

М 1:50


Кырлан Александр Сергеевич

выпуск 13.11.2026 № 6f3a8abb2c · стр. 50 из 157

План отопления

Радиаторы, стояки, подводки · размеры в мм · высоты от чистого пола

План отопления (М 1:50)

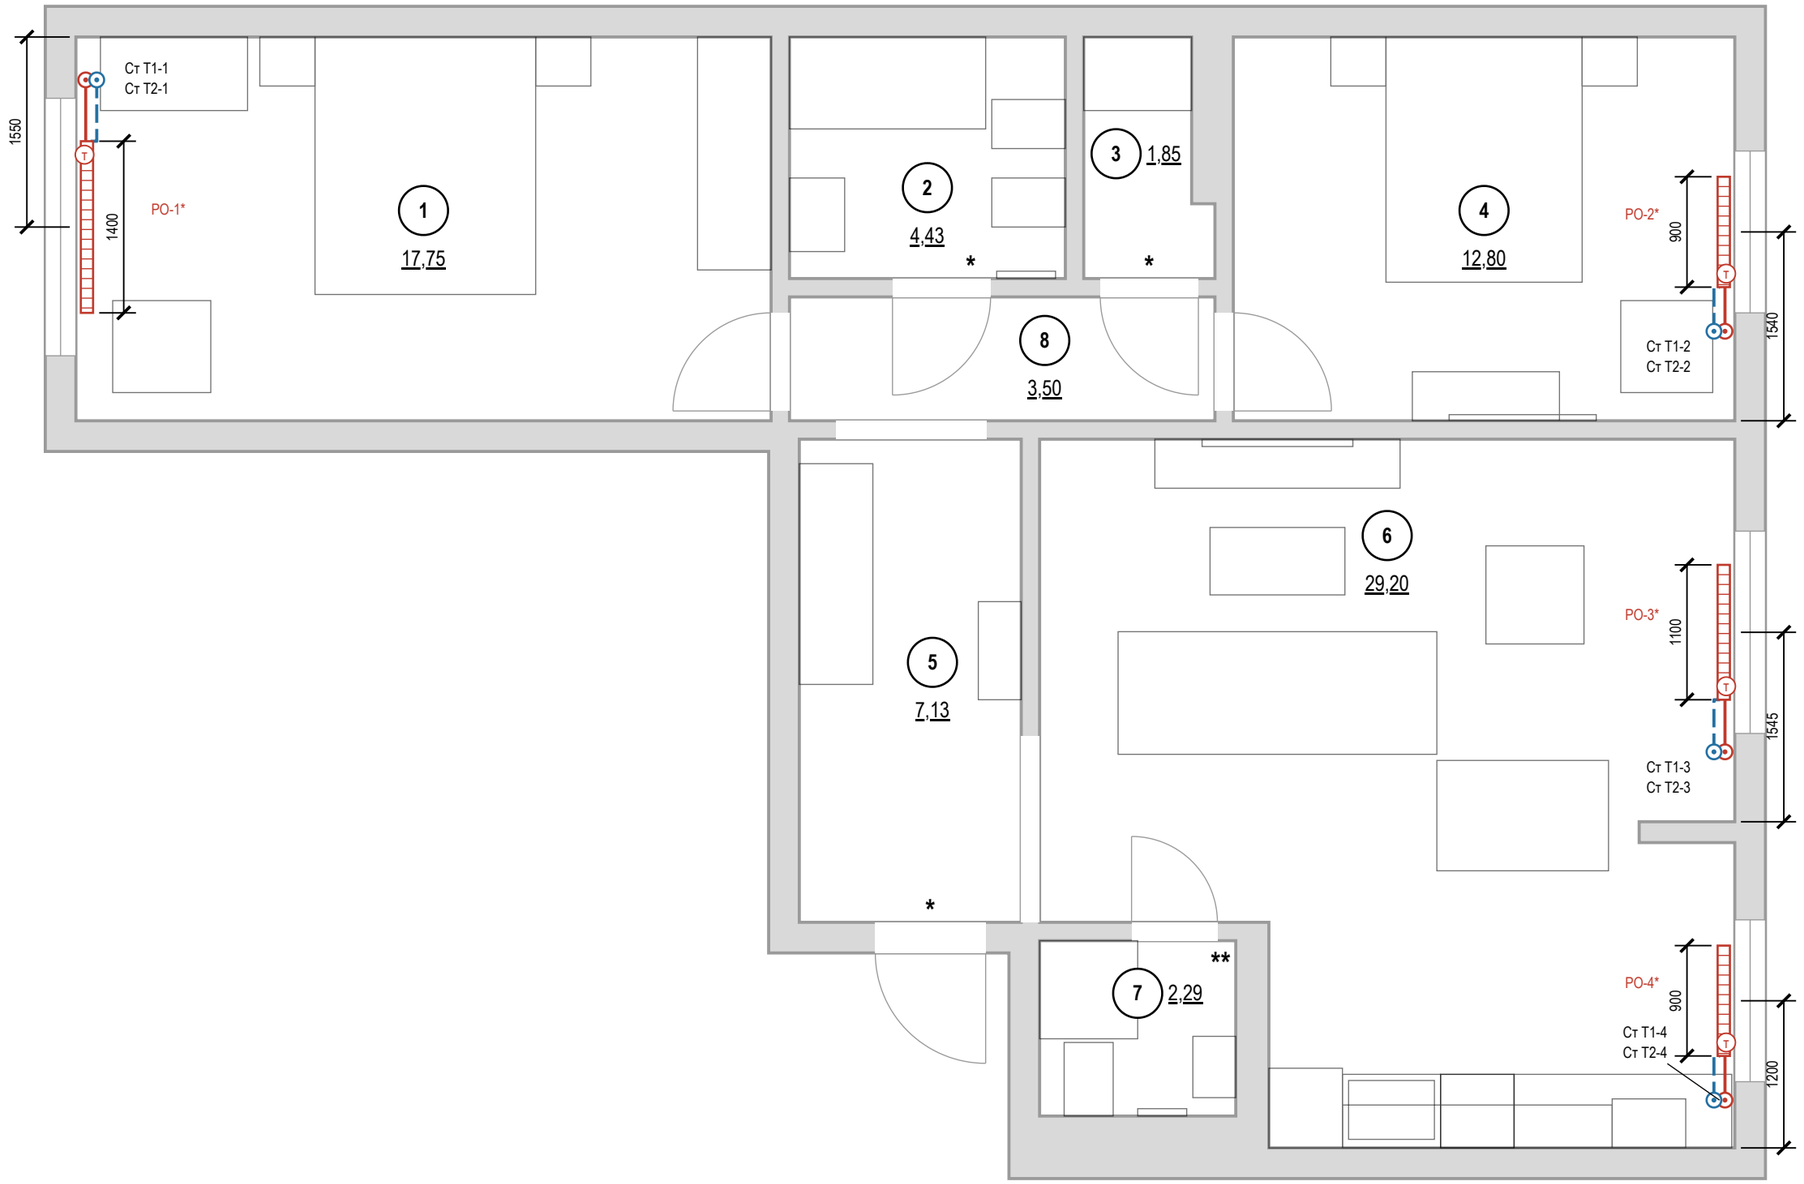

Условные обозначения

- (1) — номер помещения, площадь м²
- радиатор отопления (марка РО-N, длина по плану)
- клапан с термоголовкой на подаче
- стояк отопления, подающий (Ст Т1-N)
- стояк отопления, обратный (Ст Т2-N)
- Т1 — отопление, подающий трубопровод
- Т2 — отопление, обратный трубопровод
- * — «*» — принято, не замерено и не подтверждено
- ** — «**» — предложение проектировщика, заказчиком не утверждено

Ведомость радиаторов

Марка	Помещение	Тип	Д×В×Г, мм	Низ / стена	Q, Вт
РО-1	1. Спальня 1	панельный*	1400×600×100	120 / 40	расч.
РО-2	4. Спальня 2	панельный*	900×600×100	120 / 40	расч.
РО-3	6. Кухня-гостиная	панельный*	1100×600×100	120 / 40	расч.
РО-4	6. Кухня-гостиная	панельный*	900×600×100	120 / 40	расч.

* тип и мощность — по теплотехническому расчёту
Низ — от чистого пола, стена — зазор до задней панели, мм.

Привязки — до обмера
Стояки отопления в исходных данных не заданы: показаны у откосов окон, подводки — принципиально. До черновых работ — обмер стояков и паспорта приборов; лист перевыпустить по факту.

Допущения и предложения на листе. Основа листа: размеры сняты со скана плана заказчика по размерным цепочкам, контрольный обмер на объекте не выполнялся (К-13); высота потолка 2700 мм принята: на плане заказчика не указана (К-11); толщины стен приняты: наружные 250 мм, перегородки 150 мм (на плане 85–190 мм) (К-13); разрешённая мощность 15 кВт принята по типовой квартире, технических условий нет (К-14); утолщение стены 190 × 1360 мм и элемент 1470 × 160 мм плана заказчика не определены (К-12); ниши санузла 2 закрыты перегородкой и фальш-стеной: проектное решение, на плане заказчика ниша у входа открыта (К-18); несущие стены не определены: до технического заключения все существующие стены считаются несущими (К-20); окна существующие и сохраняются; подоконная доска и глубина откосов не заданы — приняты, не замерены (К-27); подрайон климата не задан — принят не северный (жилые от 2,5 м) (К-29). Знак «*» — принято, не замерено и не подтверждено (замерить на объекте). Знак «**» — предложение проектировщика, заказчиком не утверждено (согласовать с заказчиком). См. лист открытых вопросов (лист 7, записи К-11–К-14, К-18, К-20; лист 8, записи К-25–К-27, К-29).

Примечания

1. Расчёт системы отопления, теплопотерь и подбор приборов — проектная организация с допуском СРО; лист даёт места и привязки.
2. Тип, длина и мощность радиаторов — по теплотехническому расчёту; лист задаёт места, зазоры и подключение.
3. Радиаторы — под каждым окном жилых комнат и кухни, центр по оси проёма, длина 0,7 ширины окна (кратно 100); окончательно — по расчёту.
4. Зазоры радиатора: низ не менее 100 мм от чистого пола, верх не менее 100 мм до подоконника, 30–50 мм от стены до задней панели; центр по оси окна с допуском ±20 мм. Верх до подоконника — 180 мм.
5. Радиаторы не закрывать глухими коробами и мебелью; перенос и замена приборов в многоквартирном доме — переустройство, согласование с управляющей организацией (ЖК РФ ст. 25–26); вынос на лоджию запрещён.
6. Трубы отопления через межквартирные стены не прокладывать (СП 51.13330.2011, п. 9.19); через перекрытия и перегородки — в гильзах.
7. Привязки приборов и подводок — по паспортам приобретённых радиаторов и клапанов, до черновых работ.
8. До закрытия отделкой трубопроводы отопления испытать гидростатическим давлением с оформлением акта (СП 73.13330.2016, 7.2–7.3).
9. Знак «*» у проёма — допущение: положение проёма не замерено (дверь пом. 5, стена В; дверь пом. 8, стена А (2 шт.)); размер напечатан как принятый. Реестр: листы 6–11, вопросы К-26, К-25.

1000 мм · печать 1:1

Изм.	Кол.уч	Лист	№ док.	Подп.	Дата
Разраб.		Кырлан А.С.			13.11.26
Пров.					
ГИП					
Н. контр.					
Утв.					

ГД-2026-003-АИ

Трёхкомнатная квартира

Общая площадь 78,95* м² · * размеры со скана, не замерены (реестр — л. 6–11, К-13)

Дизайн-проект интерьера трёхкомнатной квартиры

Стадия	Лист	Листов
РП	47	132

План отопления

М 1:50

Кырлан Александр Сергеевич

выпуск 13.11.2026 № 6f3a8abb2c · стр. 51 из 157

05

Водоснабжение и канализация

Кырлан Александр Сергеевич


выпуск 13.11.2026 № 6f3a8abb2c · стр. 52 из 157

План выводов сантехники


Выводы В1, Т3, К1 · привязки от чистовых стен · высоты от чистого пола, мм

ПРЕДВАРИТЕЛЬНО · не для производства работ · открыто пунктов: 28 (реестр — л. 6–11)


Фрагмент 1. Ванная, пом. 2 (М 1:50)

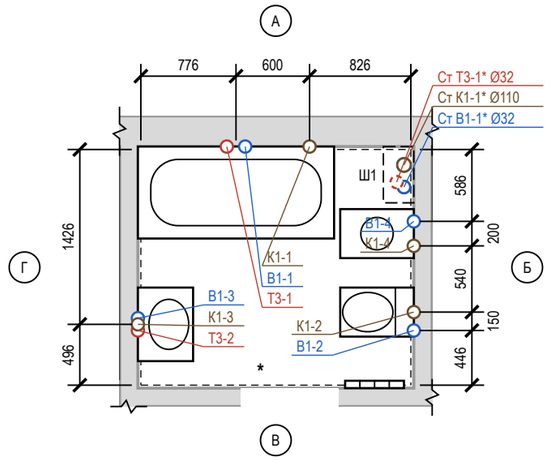

Фрагмент 2. Кухня-гостиная, пом. 6 (М 1:50)

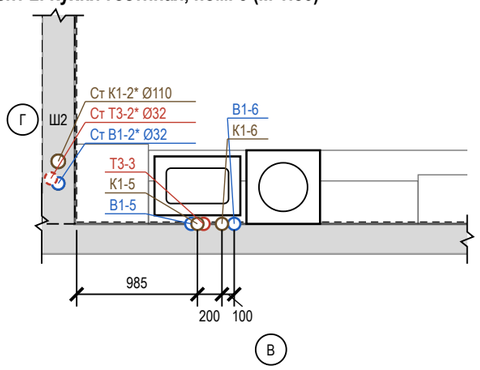

Фрагмент 3. Санузел 2, пом. 7 (М 1:50)

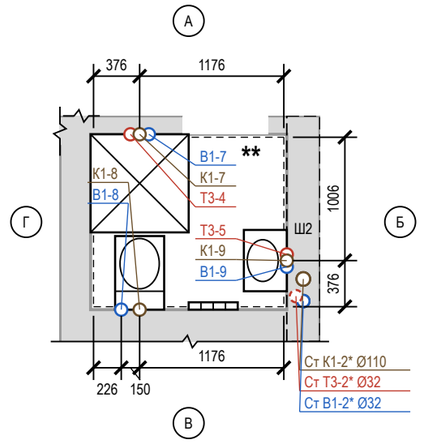

Ведомость привязок выводов

Код	Прибор	Ø	Н, мм	Привязка от чист. стен, мм	Прим.
В1-1	П1 ванна	½"	800*	ст. А: 851 от Г	межос. 150
Т3-1	—"	½"	800*	ст. А: 701 от Г	межос. 150
К1-1	—"	Ø50	50*	ст. А: 826 от Б	
В1-2	П2 унитаз подвесной	½"	250*	ст. Б: 446 от В	в раме инсталляции
К1-2	—"	Ø110	220*	ст. Б: 596 от В	
В1-3	П3 умывальник	½"	600*	ст. Г: 546 от В	межос. 100
Т3-2	—"	½"	600*	ст. Г: 446 от В	межос. 100
К1-3	—"	Ø50	500*	ст. Г: 496 от В	
В1-4	П4* стиральная машина	½"	600*	ст. Б: 586 от А	кран машины
К1-4	—"	Ø50	600*	ст. Б: 786 от А	
В1-5	П11* мойка кухонная	½"	600	ст. В: 935 от Г	межос. 100
Т3-3	—"	½"	600	ст. В: 1035 от Г	межос. 100
К1-5	—"	Ø50	400	ст. В: 985 от Г	
В1-6	П12* посудомоечная машина	½"	550	ст. В: 1285 от Г	кран ПММ в шкафу мойки
К1-6	—"	Ø40	550	ст. В: 1185 от Г	слив ПММ в шкафу мойки
В1-7	П6 душ	½"	1200*	ст. А: 451 от Г	межос. 150
Т3-4	—"	½"	1200*	ст. А: 301 от Г	межос. 150
К1-7	—"	Ø50	70*	ст. А: 376 от Г	сифон поддона
В1-8	П7 унитаз подвесной	½"	250*	ст. В: 226 от Г	в раме инсталляции
К1-8	—"	Ø110	220*	ст. В: 376 от Г	
В1-9	П8 умывальник	½"	600*	ст. Б: 326 от В	межос. 100
Т3-5	—"	½"	600*	ст. Б: 426 от В	межос. 100
К1-9	—"	Ø50	500*	ст. Б: 376 от В	

* — высота по практике монтажа; сверить по паспорту прибора

Условные обозначения

- вывод В1 (код — в ведомости привязок)
- вывод Т3 (код — в ведомости привязок)
- вывод К1 (код — в ведомости привязок)
- сантехприбор по расстановке (габарит модели)
- чистовая поверхность стены (от неё привязки)
- стояк «Ст К1-N / Ст В1-N» (ГОСТ 21.601), Ø мм
- * стояк Т3 не на обмере — принят в шахте рядом со Ст В1, сверить
- шахта / короб стояков, люк 300×400
- * у стояка — положение принято, не замерено, сверить
- линия обрыва (граница фрагмента)
- А обозначение стены А–Г (как на развёртках)

Примечания

1. Привязки выводов даны от чистовых поверхностей стен (облицовка на сторону: ванная — 24 мм (штукатурка 10 + клей 5 + плитка 9); кухня-гостиная — 24 мм (фартук: штукатурка 10 + клей 5 + плитка 9); санузел 2 — 24 мм (штукатурка 10 + клей 5 + плитка 9)); эти же грани — на развёртках и в раскладке плитки. Высоты — от чистого пола помещения.
2. Высоты и межосевые, отмеченные «*», приняты по практике монтажа; до черновой разводки сверить по паспорту выбранного прибора (смеситель, инсталляция, сифон).
3. Горячая вода (Т3) — слева от холодной (В1), если смотреть на прибор. Допуск установки выводов: ±5 мм в группе, ±20 мм у отдельно стоящих.
4. Расчёт систем водоснабжения и канализации и подбор оборудования выполняет проектная организация; лист задаёт места и высоты выводов.
5. Посудомоечная машина П12*: кран и слив — отдельными выводами в шкафу мойки (не за машиной), до машины ≤ 1500 мм.
6. Ст Т3-1, Ст Т3-2 на обмере не показаны: приняты рядом с Ст В1-1*, Ст В1-2* (в МКД стоят группой); положение сверить на объекте до разметки.
7. Стояки в коробах/шахтах Ш1, Ш2 не замоноличивать; стояк К1 в коробе — звукоизоляция стояка в коробе без жёсткого контакта с трубой; к арматуре и ревизиям — люк не меньше 300×400.
8. Допущение проекта: санузел 2 — проектное решение: ниша 1600 × 1840 у входа (на плане открыта в кухню-гостиную) закрыта перегородкой по линии низа прихожей; ниша 660 × 260 у наружной стены (уступ по плану) закрыта фальш-стеной по линии уступа, в ней рама инсталляции унитаза.
9. Допущение проекта: стояки: у ванной — в коробе Ш1 248 × 459; у санузла 2 — в стене-пилоне 270 мм (Ш2) между санузлом 2 и кухней; люки 300 × 400; положение стояков условно — сверить на объекте.
10. Допущение проекта: кухня: раскладка гарнитура принята проектной, решение автора (ИЗ-12) — мойка М7* у шахты Ш2, ПММ М14* рядом с мойкой, варочная и духовой шкаф в М8*, вытяжка М15**, холодильник М6**; выводы техники — по типовой расстановке; условие: до начала черновых работ сверить раскладку и выводы с чертежом кухни от изготовителя, выводы пересматриваются по его чертежу (вопрос К-8).
11. Допущение проекта: стиральная машина П4* — вертикальной загрузки, габарит в плане 400 × 600 мм (ширина 400 вдоль стены Б): условие закупки, а не пожелание, решение автора (ИЗ-11); машина с фронтальной загрузкой или большего габарита не подходит — перед люком ванна П1; модель не выбрана, габарит и подводку сверить по паспорту до закрытия трасс (вопрос К-19).
12. Марки из допущений, которых нет на этом листе: М6**, М7*, М8*, М14*, М15** — лист 77.
13. Знак «*» у стояка — положение принято, не замерено (все стояки); сверить на объекте до разметки. Реестр: листы 6–11, вопрос К-17.

1000 мм · печать 1:1

Допущения и предложения на листе. Основа листа: размеры сняты со скана плана заказчика по размерным цепочкам, контрольный обмер на объекте не выполнялся (К-13); высота потолка 2700 мм принята: на плане заказчика не указана (К-11); толщины стен приняты: наружные 250 мм, перегородки 150 мм (на плане 85–190 мм) (К-13); разрешённая мощность 15 кВт принята по типовой квартире, технических условий нет (К-14); утолщение стены 190 × 1360 мм и элемент 1470 × 160 мм плана заказчика не определены (К-12); ниши санузла 2 закрыты перегородкой и фальш-стеной: проектное решение, на плане заказчика ниша у входа открыта (К-18); несущие стены не определены: до технического заключения все существующие стены считаются несущими (К-20); окна существующие и сохраняются; подоконная доска и глубина откосов не заданы — приняты, не замерены (К-27); подрайон климата не задан — принят не северный (жилые от 2,5 м) (К-29). Знак «*» — принято, не замерено (замерить): ИЗ-11, К-19: П4; К-8: М8, П11. Знак «**» — предложено, не утверждено (согласовать). См. лист открытых вопросов (лист 6, записи К-1, К-5, К-8; лист 7, записи К-11–К-14, К-17–К-20; лист 8, записи К-25, К-27, К-29; лист 9, запись ИЗ-5; лист 10, запись ИЗ-11).


						ГД-2026-003-АИ
						Трёхкомнатная квартира
Изм.	Кол.уч	Лист	№ док.	Подп.	Дата	Общая площадь 78,95* м² · * размеры со скана, не замерены (реестр — л. 6–11, К-13)
Разраб.		Кырлан А.С.			13.11.26	Дизайн-проект интерьера трёхкомнатной квартиры
Пров.						Стадия: РП · Лист: 48 · Листов: 132
ГИП						**План выводов сантехники**
						М 1:50
Н. контр.						**Кырлан Александр Сергеевич**
Утв.						

выпуск 13.11.2026 № 6f3a8abb2c · стр. 53 из 157


Схема разводки водопровода и канализации

Схемы систем В1, Т3, К1 · трассы принципиальные · уклоны в мм на 1 м · план М 1:200, фрагменты М 1:40

План квартиры (М 1:200)

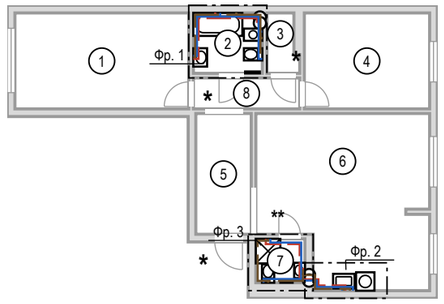


Узел ввода В1, Т3 (схема, без масштаба)

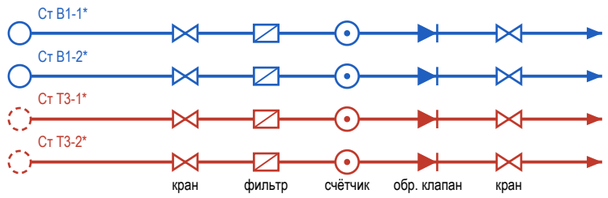


состав узла — по согласованию

⊗ Ст К1-1*, Ст К1-2*: ревизия на стояке — люк в коробе


Фр. 1. Ванная (М 1:40)

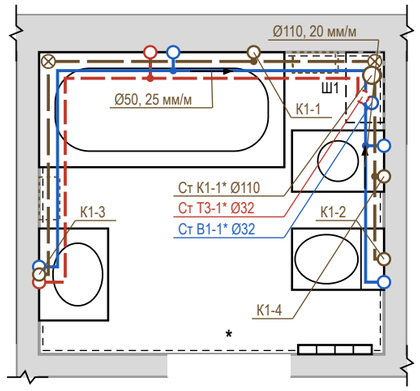

Фр. 2. Кухня-гостиная (М 1:40)

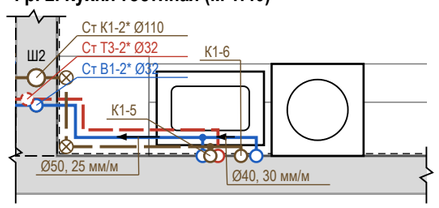

Фр. 3. Санузел 2 (М 1:40)

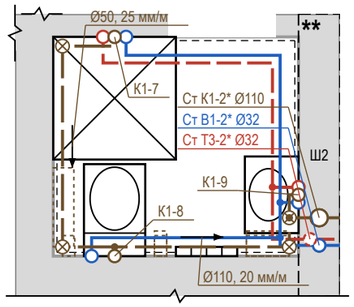

Условные обозначения

- В1 — водопровод хозяйственно-питьевой (ХВС), PP-R Ø20
- Т3 — горячее водоснабжение, подача (ГВС), PP-R Ø20
- К1 — канализация бытовая
- направление уклона К1 / пола: Ø, мм на 1 м
- ⊗ ревизия (прочистка) К1 — доступ сохранить
- • тройник (ответвление к прибору)
- короб К1 над чистым полом (ГКЛВ под плитку)
- ○ вывод В1 (код — в ведомости привязок)
- ○ вывод Т3 (код — в ведомости привязок)
- ○ вывод К1 (код — в ведомости привязок)
- сантехприбор по расстановке (габарит модели)
- ○ стояк «Ст К1-N / Ст В1-N» (ГОСТ 21.601), Ø мм
- * стояк Т3 не на обмере — принят в шахте рядом со Ст В1, сверить
- * у стояка — положение принято, не замерено, сверить
- шахта / короб стояков, люк 300×400
- линия обрыва (граница фрагмента)
- граница фрагмента на плане (Фр. N)

Профиль выпусков К1 (до врезки в стояк)

Выпуск	Прибор	Ø	L, м	i, мм/м	Δh, мм	Прокладка, мм
К1-8	П7 унитаз подвесной	Ø110	1,58	20	32	короб 180×140
К1-2	П2 унитаз подвесной	Ø110	1,28	20	26	над полом за приборами
К1-3	П3 умывальник	Ø50	3,69	25	92	короб 180×110
К1-7	П6 душ	Ø50	3,58	25	89	короб 170×110
К1-5	П11* мойка кухонная	Ø50	1,65	25	41	над полом за приборами
К1-1	П1 ванна	Ø50	0,96	25	24	короб 110×110
К1-4	П4* стиральная машина	Ø50	0,74	25	19	над полом за приборами
К1-9	П8 умывальник	Ø50	0,41	25	10	над полом за приборами
К1-6	П12* посудомоечная машина	Ø40	1,84	30	55	над полом за приборами

Короб h×b: h — от чистого пола, b — от чистовой стены. Стяжка 35 мм — лист полов.

Примечания

1. Трассы принципиальные, построены от стояков вдоль стен помещений; фактическое положение фиксируется исполнительной схемой с привязками (фото с рулеткой) до закрытия.
2. Уклон К1 не менее 1/d и не более 150 мм/м (СП 30.13330.2020, п. 19.1), приняты практические уклоны; поворот — двумя отводами 45°, ревизия после поворота, доступ сохранить. Стояк К1 в коробе — звукоизоляция стояка в коробе, без жёсткого контакта короба с трубой.
3. Решение по К1: стяжка 35 мм не укрывает трубы (нужно Ø + Δh + 45 мм) — выпуски идут над чистым полом вдоль стен: К1-2, К1-5, К1-4, К1-9, К1-6 — за приборами и в раме инсталляции; К1-8, К1-3, К1-7, К1-1 — в коробе ГКЛВ под плитку (размеры в профиле). Короба — на развёртках; отметку низа врезки в стояк замерить до черновых работ.
4. Состав узла ввода В1, Т3 — по согласованию: на схеме типовой узел — кран шаровой, фильтр, счётчик, обратный клапан, кран; состав и места не определены (записи реестра нет). Доступ к арматуре — через люк не меньше 300×400. Водопровод — в штробе стен или в коробах; трубы испытать давлением до закрытия (акт скрытых работ).
5. Расчёт систем, диаметры магистралей и подбор оборудования выполняет проектная организация; врезка и перенос стояков — по согласованию с управляющей организацией. Арматуру и привязки сверить по паспортам приборов.
6. Ведомость выводов (код, прибор, высота, привязка) — лист 48; на схеме — только коды.
7. Ст Т3-1, Ст Т3-2 на обмере не показаны: приняты рядом с Ст В1-1*, Ст В1-2* (в МКД стоят группой); положение сверить на объекте до разводки.
8. Допущение проекта: санузел 2 — проектное решение: ниша 1600 × 1840 у входа (на плане открыта в кухню-гостиную) закрыта перегородкой по линии низа прихожей; ниша 660 × 260 у наружной стены (уступ по плану) закрыта фальш-стеной по линии уступа, в ней рама инсталляции унитаза.
9. Допущение проекта: стояки: у ванной — в коробе Ш1 248 × 459; у санузла 2 — в стене-пилоне 270 мм (Ш2) между санузлом 2 и кухней; люки 300 × 400; положение стояков условно — сверить на объекте.
10. Допущение проекта: кухня: раскладка гарнитура принята проектной, решение автора (ИЗ-12) — мойка М7* у шахты Ш2, ПММ М14* рядом с мойкой, варочная и духовой шкаф в М8*, вытяжка М15**, холодильник М6**; выводы техники — по типовой расстановке; условие: до начала черновых работ сверить раскладку и выводы с чертежом кухни от изготовителя, выводы пересматриваются по его чертежу (вопрос К-8).
11. Допущение проекта: стиральная машина П4* — вертикальной загрузки, габарит в плане 400 × 600 мм (ширина 400 вдоль стены Б): условие закупки, а не пожелание, решение автора (ИЗ-11); машина с фронтальной загрузкой или большего габарита не подходит — перед люком ванна П1; модель не выбрана, габарит и подводку сверить по паспорту до закрытия трасс (вопрос К-19).
12. Марки из допущений, которых нет на этом листе: М6**, М7*, М8*, М14*, М15** — лист 77.
13. Знак «*» у стояка — положение принято, не замерено (все стояки); сверить на объекте до разметки. Реестр: листы 6–11, вопрос К-17.

Допущения и предложения на листе. Основа листа: размеры сняты со скана плана заказчика по размерным цепочкам, контрольный обмер на объекте не выполнялся (К-13); высота потолка 2700 мм принята: на плане заказчика не указана (К-11); толщины стен приняты: наружные 250 мм, перегородки 150 мм (на плане 85–190 мм) (К-13); разрешённая мощность 15 кВт принята по типовой квартире, технических условий нет (К-14); утолщение стены 190 × 1360 мм и элемент 1470 × 160 мм плана заказчика не определены (К-12); ниши санузла 2 закрыты перегородкой и фальш-стеной: проектное решение, на плане заказчика ниша у входа открыта (К-18); несущие стены не определены: до технического заключения все существующие стены считаются несущими (К-20); окна существующие и сохраняются; подоконная доска и глубина откосов не заданы — приняты, не замерены (К-27); подрайон климата не задан — принят не северный (жилые от 2,5 м) (К-29). Знак «*» — принято, не замерено и не подтверждено (замерить на объекте): ИЗ-11, К-19: П4 — вертикальная загрузка 400 × 600 мм — условие закупки (решение автора, ИЗ-11); модель не выбрана, габарит сверить по паспорту; К-8: М8 — Ряд М6…М8 стена-в-стену: было 600+800+600+1800 = 3800 от х 9730 до черновой грани стены Б (13530); чистовая длина стены по развёртке 3770 (отделка 15/15) — гарнитур длиннее стены на 30 мм, зазора под компенсатор нет; П11 — Размер мойки — один источник: вырез в столешнице М7 на плане столешницы и в ведомости техники 700×480, в данных прибора было 500×450. Знак «**» — предложение проектировщика, заказчиком не утверждено (согласовать с заказчиком). См. лист открытых вопросов (лист 6, запись К-8; лист 7, записи К-11–К-14, К-17–К-20; лист 8, записи К-25–К-27, К-29; лист 9, запись ИЗ-5; лист 10, запись ИЗ-11); по листу — К-17.


Изм.	Кол.уч	Лист	№ док.	Подп.	Дата	ГД-2026-003-АИ			
						Трёхкомнатная квартира			
						Общая площадь 78,95* м² · * размеры со скана, не замерены (реестр — л. 6–11, К-13)			
Разраб.		Кырлан А.С.			13.11.26	Дизайн-проект интерьера трёхкомнатной квартиры	Стадия	Лист	Листов
Пров.							РП	49	132
ГИП									
Н. контр.						Схема разводки водопровода и канализации	Кырлан Александр Сергеевич		
Утв.						М 1:200; 1:40			

выпуск 13.11.2026 № 6f3a8abb2c · стр. 54 из 157

Аксонометрическая схема В1 (холодное водоснабжение)

аксонометрия · диаметры, уклоны, отметки, стояки и приборы · трассы принципиальные

Схема В1 (М 1:100)

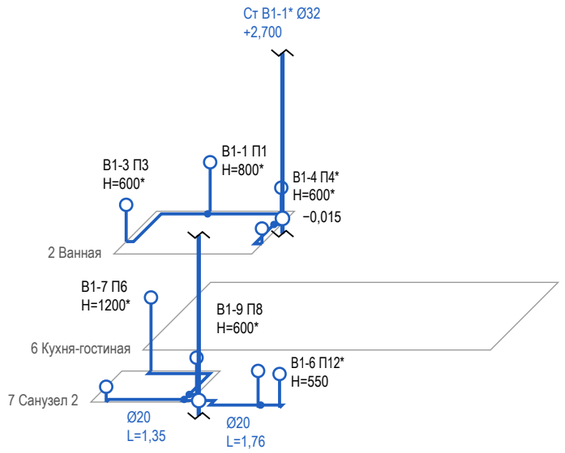

Ведомость выводов В1

Код	Прибор	H, мм	Ø, мм	Трасса, м
В1-3	П3 умывальник	600*	20	3,66
В1-7	П6 душ	1200*	20	2,62
В1-6	П12* посудомоечная машина	550	20	1,76
В1-8	П7 унитаз подвесной	250*	20	1,35
В1-1	П1 ванна	800*	20	0,12
В1-5	П11* мойка кухонная	600	20	0,12
В1-2	П2 унитаз подвесной	250*	20	1,29
В1-9	П8 умывальник	600*	20	0,12
В1-4	П4* стиральная машина	600*	20	0,12

Допущения и предложения на листе. Знак «*» принято (замерить): Ст К1-1, Ст К1-2, Ст В1-2. Знак «**» предложено (согласовать). См. лист открытых вопросов (листы 6–11).

Примечания

1. Схема В1 построена по тем же трассам, что план разводки: положение в плане сохранено, глубина — в масштабе ×0,5. Трассы принципиальные; фактическое положение фиксируется исполнительной схемой до закрытия.
2. Высоты H — от чистого пола помещения, мм. Отметка прокладки магистрали В1 (в стяжке, в стене или по полу) в данных не задана: участки показаны на уровне пола условно (записи реестра нет).
3. * — высота вывода принята по практике монтажа; сверить по паспорту прибора.
4. Узел ввода В1 (кран, фильтр, счётчик, обратный клапан, кран) — на схеме разводки; состав узла ввода — по согласованию. Кран шаровой — на первом участке от стояка.
5. Допущение проекта: санузел 2 — проектное решение: ниша 1600 × 1840 у входа (на плане открыта в кухню-гостиную) закрыта перегородкой по линии низа прихожей; ниша 660 × 260 у наружной стены (уступ по плану) закрыта фальш-стеной по линии уступа, в ней рама инсталляции унитаза.
6. Допущение проекта: стояки: у ванной — в коробе Ш1 248 × 459; у санузла 2 — в стене-пилоне 270 мм (Ш2) между санузлом 2 и кухней; люки 300 × 400; положение стояков условно — сверить на объекте.
7. Допущение проекта: кухня: раскладка гарнитура принята проектной, решение автора (ИЗ-12) — мойка М7* у шахты Ш2, ПММ М14* рядом с мойкой, варочная и духовой шкаф в М8*, вытяжка М15**, холодильник М6**; выводы техники — по типовой расстановке; условие: до начала черновых работ сверить раскладку и выводы с чертежом кухни от изготовителя, выводы пересматриваются по его чертежу (вопрос К-8).
8. Допущение проекта: стиральная машина П4* — вертикальной загрузки, габарит в плане 400 × 600 мм (ширина 400 вдоль стены Б): условие закупки, а не пожелание, решение автора (ИЗ-11); машина с фронтальной загрузкой или большего габарита не подходит — перед люком ванна П1; модель не выбрана, габарит и подводку сверить по паспорту до закрытия трасс (вопрос К-19).
9. Марки из допущений, которых нет на этом листе: М6**, М7*, М8*, М14*, М15** — лист 77.
10. Трубы испытать давлением до закрытия (акт скрытых работ, опрессовка по СП 73.13330.2016).
11. Диаметры, высоты выводов и места кранов — по паспортам выбранных приборов и расчёту проектной организации.
12. Расчёт систем, диаметры магистралей и подбор оборудования выполняет проектная организация.

1000 мм · печать 1:1

Условные обозначения

- В1 — водопровод хозяйственно-питьевой (ХВС), PP-R Ø20
- вывод В1 (код — в ведомости привязок)
- стояк «Ст К1-N / Ст В1-N» (ГОСТ 21.601), Ø мм
- стояк в плане (на отметке пола); вертикаль — стояк по высоте, разрыв — перекрытие
- тройник (ответвление к прибору)
- кран шаровой

ПРЕДВАРИТЕЛЬНО · не для производства работ · открыто пунктов: 28 (реестр — л. 6–11)

Изм.	Кол.уч	Лист	№ док.	Подп.	Дата
Разраб.		Кырлан А.С.			13.11.26
Пров.					
ГИП					
Н. контр.					
Утв.					

ГД-2026-003-АИ

Трёхкомнатная квартира

Общая площадь 78,95* м² · * размеры со скана, не замерены (реестр — л. 6–11, К-13)

Дизайн-проект интерьера трёхкомнатной квартиры

Стадия	Лист	Листов
РП	50	132

Аксонометрическая схема В1 (холодное водоснабжение)

М 1:100


Кырлан Александр Сергеевич

выпуск 13.11.2026 № 6f3a8abb2c · стр. 55 из 157

Аксонометрическая схема Т3 (горячее водоснабжение)

аксонометрия · диаметры, уклоны, отметки, стояки и приборы · трассы принципиальные

Схема Т3 (М 1:100)

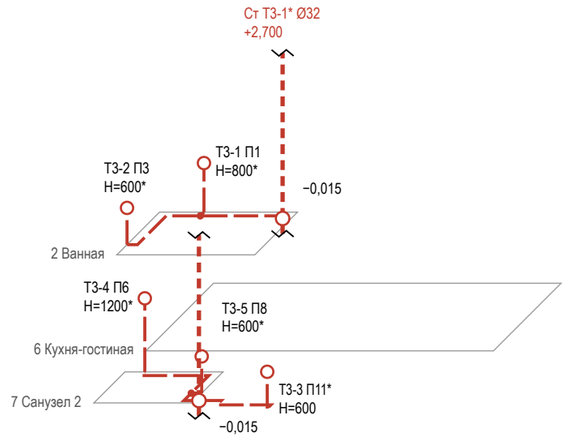

Ведомость выводов Т3

Код	Прибор	H, мм	Ø, мм	Трасса, м
Т3-2	П3 умывальник	600*	20	3,56
Т3-4	П6 душ	1200*	20	2,67
Т3-1	П1 ванна	800*	20	0,17
Т3-3	П11* мойка кухонная	600	20	1,61
Т3-5	П8 умывальник	600*	20	0,17

Условные обозначения

- Т3 — горячее водоснабжение, подача (ГВС), PP-R Ø20
- вывод Т3 (код — в ведомости привязок)
- стояк «Ст К1-N / Ст В1-N» (ГОСТ 21.601), Ø мм
- стояк в плане (на отметке пола); вертикаль — стояк по высоте, разрыв — перекрытие
- тройник (ответвление к прибору)
- кран шаровой
- * стояк Т3 не на обмере — принят в шахте рядом со Ст В1, сверить

Допущения и предложения на листе. Знак «*» принято (замерить): Ст К1-1, Ст К1-2. Знак «**» предложено (согласовать). См. лист открытых вопросов (листы 6–11).

Примечания

1. Схема Т3 построена по тем же трассам, что план разводки: положение в плане сохранено, глубина — в масштабе ×0,5. Трассы принципиальные; фактическое положение фиксируется исполнительной схемой до закрытия.
2. Высоты H — от чистого пола помещения, мм. Отметка прокладки магистрали Т3 (в стяжке, в стене или по полу) в данных не задана: участки показаны на уровне пола условно (записи реестра нет).
3. * — высота вывода принята по практике монтажа; сверить по паспорту прибора.
4. Узел ввода Т3 (кран, фильтр, счётчик, обратный клапан, кран) — на схеме разводки; состав узла ввода — по согласованию. Кран шаровой — на первом участке от стояка.
5. Циркуляция ГВС в данных не задана — циркуляционного трубопровода на схеме нет (записи реестра нет).
6. Ст Т3-1, Ст Т3-2 на обмере не показаны: приняты рядом с Ст В1-1*, Ст В1-2* (в МКД стоят группой); положение сверить на объекте до разводки.
7. Допущение проекта: санузел 2 — проектное решение: ниша 1600 × 1840 у входа (на плане открыта в кухню-гостиную) закрыта перегородкой по линии низа прихожей; ниша 660 × 260 у наружной стены (уступ по плану) закрыта фальш-стеной по линии уступа, в ней рама инсталляции унитаза.
8. Допущение проекта: стояки: у ванной — в коробе Ш1 248 × 459; у санузла 2 — в стене-пилоне 270 мм (Ш2) между санузлом 2 и кухней; люки 300 × 400; положение стояков условно — сверить на объекте.
9. Допущение проекта: кухня: раскладка гарнитура принята проектной, решение автора (ИЗ-12) — мойка М7* у шахты Ш2, ПММ М14* рядом с мойкой, варочная и духовой шкаф в М8*, вытяжка М15**, холодильник М6**; выводы техники — по типовой расстановке; условие: до начала черновых работ сверить раскладку и выводы с чертежом кухни от изготовителя, выводы пересматриваются по его чертежу (вопрос К-8).
10. Допущение проекта: стиральная машина П4* — вертикальной загрузки, габарит в плане 400 × 600 мм (ширина 400 вдоль стены Б): условие закупки, а не пожелание, решение автора (ИЗ-11); машина с фронтальной загрузкой или большего габарита не подходит — перед люком ванна П1; модель не выбрана, габарит и подводку сверить по паспорту до закрытия трасс (вопрос К-19).
11. Марки из допущений, которых нет на этом листе: М6**, М7*, М8*, М14*, М15** — лист 77.
12. Трубы испытать давлением до закрытия (акт скрытых работ, опрессовка по СП 73.13330.2016).
13. Диаметры, высоты выводов и места кранов — по паспортам выбранных приборов и расчёту проектной организации.
14. Расчёт систем, диаметры магистралей и подбор оборудования выполняет проектная организация.

1000 мм · печать 1:1

Изм.	Кол.уч	Лист	№ док.	Подп.	Дата
Разраб.		Кырлан А.С.			13.11.26
Пров.					
ГИП					
Н. контр.					
Утв.					

ГД-2026-003-АИ

Трёхкомнатная квартира

Общая площадь 78,95* м² · * размеры со скана, не замерены (реестр — л. 6–11, К-13)

Дизайн-проект интерьера трёхкомнатной квартиры

Стадия	Лист	Листов
РП	51	132

Аксонометрическая схема Т3 (горячее водоснабжение)

М 1:100


Кырлан Александр Сергеевич

выпуск 13.11.2026 № 6f3a8abb2c · стр. 56 из 157

Аксонометрическая схема К1 (канализация)

аксонометрия · диаметры, уклоны, отметки, стояки и приборы · трассы принципиальные

Схема К1 (М 1:100)

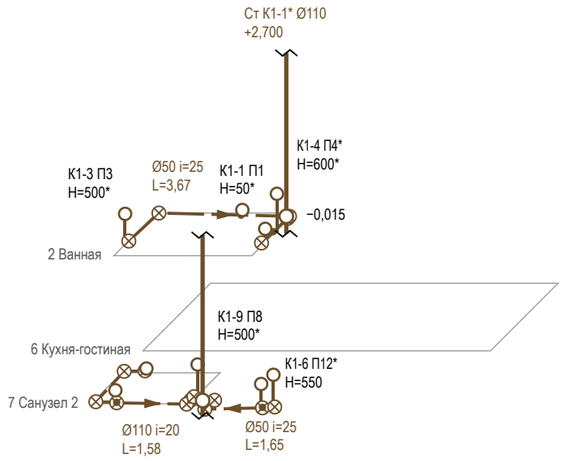

ПРЕДВАРИТЕЛЬНО · не для производства работ · открыто пунктов: 28 (реестр — л. 6–11)

Ведомость выводов К1

Код	Прибор	Н, мм	Ø, i	Трасса, м
К1-8	П7 унитаз подвесной	220*	110 i=20	1,58
К1-2	П2 унитаз подвесной	220*	110 i=20	1,28
К1-3	П3 умывальник	500*	50 i=25	3,67
К1-7	П6 душ	70*	50 i=25	2,05
К1-5	П11* мойка кухонная	400	50 i=25	1,65
К1-1	П1 ванна	50*	50 i=25	0,06
К1-4	П4* стиральная машина	600*	50 i=25	0,06
К1-9	П8 умывальник	500*	50 i=25	0,21
К1-6	П12* посудомоечная машина	550	40 i=30	0,26

Условные обозначения

- К1 — канализация бытовая
- вывод К1 (код — в ведомости привязок)
- стояк «Ст К1-N / Ст В1-N» (ГОСТ 21.601), Ø мм
- стояк в плане (на отметке пола); вертикаль — стояк по высоте, разрыв — перекрытие
- направление уклона К1 / пола: Ø, мм на 1 м
- ⊗ ревизия (прочистка) К1 — доступ сохранить
- • тройник (ответвление к прибору)

Допущения и предложения на листе. Знак «*» принято (замерить): Ст В1-1, Ст К1-2, Ст В1-2. Знак «**» предложено (согласовать). См. лист открытых вопросов (листы 6–11).

Примечания

1. Схема К1 построена по тем же трассам, что план разводки: положение в плане сохранено, глубина — в масштабе ×0,5. Трассы принципиальные; фактическое положение фиксируется исполнительной схемой до закрытия.
2. Отметки — от плиты перекрытия: низ трубы у врезки в стояк — отметка из данных выпуска, к прибору труба поднимается на уклон i, мм/м (уклон не менее 1/d и не более 150 мм/м, СП 30.13330.2020, п. 19.1); чистый пол — выше плиты на стяжку (высота пирога пола). Высота выпуска прибора Н — от чистого пола.
3. * — высота вывода принята по практике монтажа; сверить по паспорту прибора.
4. Ревизия — на повороте и в начале участка; стояк К1 в коробе с люком — звукоизоляция стояка в коробе; поворот — двумя отводами 45°.
5. Допущение проекта: санузел 2 — проектное решение: ниша 1600 × 1840 у входа (на плане открыта в кухню-гостиную) закрыта перегородкой по линии низа прихожей; ниша 660 × 260 у наружной стены (уступ по плану) закрыта фальш-стеной по линии уступа, в ней рама инсталляции унитаза.
6. Допущение проекта: стояки: у ванной — в коробе Ш1 248 × 459; у санузла 2 — в стене-пилоне 270 мм (Ш2) между санузлом 2 и кухней; люки 300 × 400; положение стояков условно — сверить на объекте.
7. Допущение проекта: кухня: раскладка гарнитура принята проектной, решение автора (ИЗ-12) — мойка М7* у шахты Ш2, ПММ М14* рядом с мойкой, варочная и духовой шкаф в М8*, вытяжка М15**, холодильник М6**; выводы техники — по типовой расстановке; условие: до начала черновых работ сверить раскладку и выводы с чертежом кухни от изготовителя, выводы пересматриваются по его чертежу (вопрос К-8).
8. Допущение проекта: стиральная машина П4* — вертикальной загрузки, габарит в плане 400 × 600 мм (ширина 400 вдоль стены Б): условие закупки, а не пожелание, решение автора (ИЗ-11); машина с фронтальной загрузкой или большего габарита не подходит — перед люком ванна П1; модель не выбрана, габарит и подводку сверить по паспорту до закрытия трасс (вопрос К-19).
9. Марки из допущений, которых нет на этом листе: М6**, М7*, М8*, М14*, М15** — лист 77.
10. Трубы испытать давлением до закрытия (акт скрытых работ, опрессовка по СП 73.13330.2016).
11. Диаметры, высоты выводов и места кранов — по паспортам выбранных приборов и расчёту проектной организации.
12. Расчёт систем, диаметры магистралей и подбор оборудования выполняет проектная организация.

1000 мм · печать 1:1

Изм.	Кол.уч	Лист	№ док.	Подп.	Дата
Разраб.		Кырлан А.С.			13.11.26
Пров.					
ГИП					
Н. контр.					
Утв.					

ГД-2026-003-АИ

Трёхкомнатная квартира

Общая площадь 78,95* м² · * размеры со скана, не замерены (реестр — л. 6–11, К-13)

Дизайн-проект интерьера трёхкомнатной квартиры

Стадия	Лист	Листов
РП	52	132

Аксонометрическая схема К1 (канализация)

М 1:100

Кырлан Александр Сергеевич


выпуск 13.11.2026 № 6f3a8abb2c · стр. 57 из 157

Развёртки мокрых зон: выводы ВК. Ванная


пом. 2 · выводы В1, Т3, К1 на стенах · высоты от чистого пола, привязки от чистовых углов, мм

ПРЕДВАРИТЕЛЬНО · не для производства работ · открыто пунктов: 28 (реестр — л. 6–11)


Стена А (М 1:20)

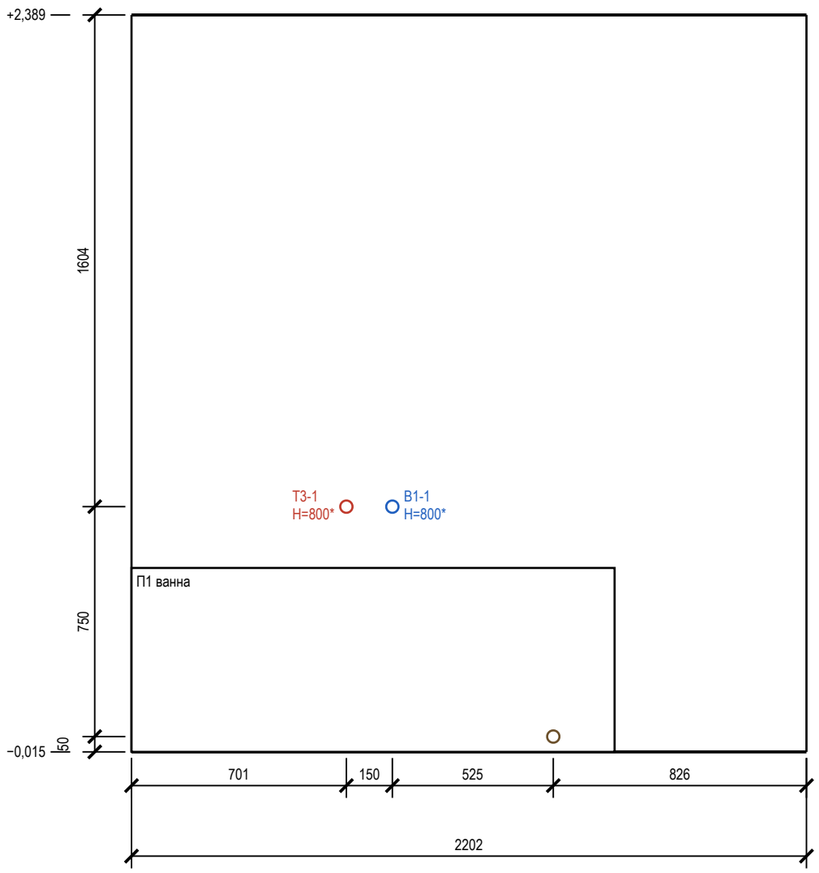

Стена Б (М 1:20)

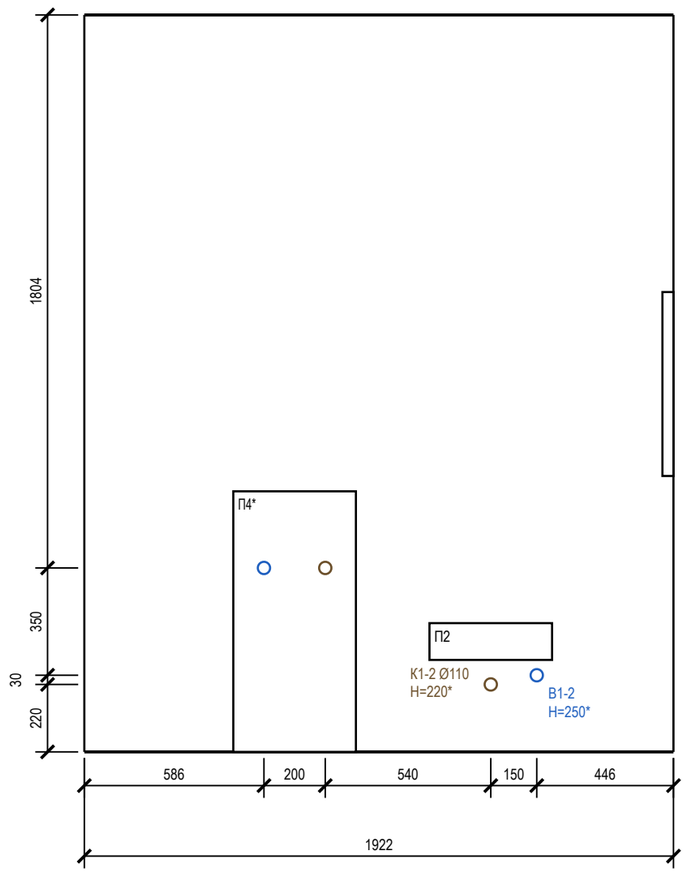

Стена Г (М 1:20)

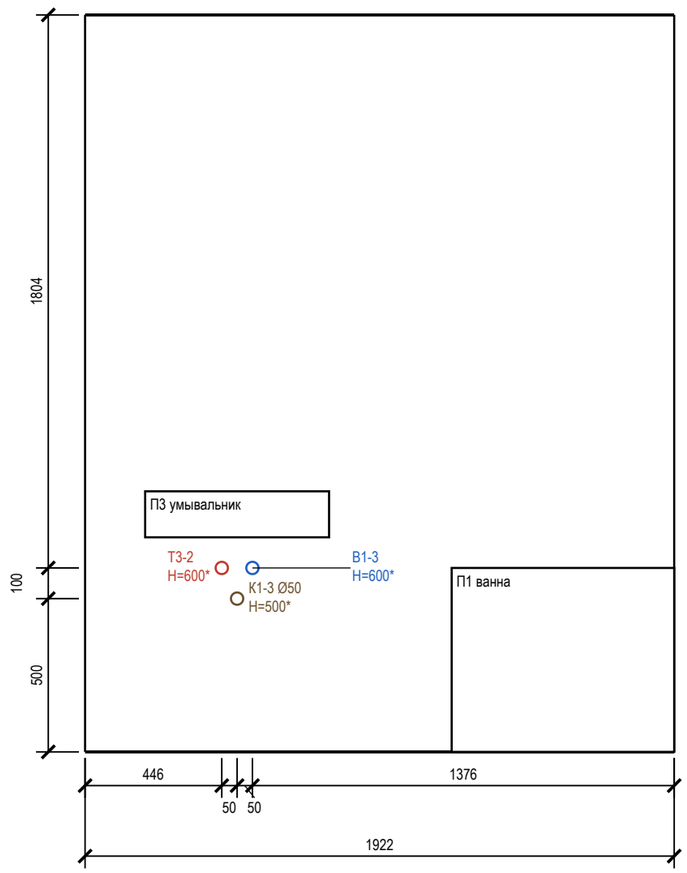

Ведомость привязок выводов (от чистого пола и угла)

Код	Прибор	Ø	Н, мм	Привязка, мм
В1-1	П1 ванна	½"	800*	ст. А: 851 от лев. угла
Т3-1	П1 ванна	½"	800*	ст. А: 701 от лев. угла
К1-1	П1 ванна	Ø50	50*	ст. А: 1376 от лев. угла
В1-2	П2 унитаз подвесной	½"	250*	ст. Б: 1476 от лев. угла
К1-2	П2 унитаз подвесной	Ø110	220*	ст. Б: 1326 от лев. угла

Ведомость привязок (продолжение)

Код	Прибор	Ø	Н, мм	Привязка, мм
В1-4	П4* стиральная машина	½"	600*	ст. Б: 586 от лев. угла
К1-4	П4* стиральная машина	Ø50	600*	ст. Б: 786 от лев. угла
В1-3	П3 умывальник	½"	600*	ст. Г: 546 от лев. угла
Т3-2	П3 умывальник	½"	600*	ст. Г: 446 от лев. угла
К1-3	П3 умывальник	Ø50	500*	ст. Г: 496 от лев. угла

Условные обозначения

- вывод В1 (код — в ведомости привязок)
- вывод Т3 (код — в ведомости привязок)
- вывод К1 (код — в ведомости привязок)
- сантехприбор по расстановке (габарит модели)
- дверной проём; окно — сплошной контур

Допущения и предложения на листе. Знак «*» принято (замерить). См. лист открытых вопросов (листы 6–11).

Примечания

1. Габариты и высоты приборов, межосевые смесителей и места кранов — по паспортам выбранных приборов, сверяются до разметки стен.
2. Высоты Н — от чистого пола помещения, мм; отметка чистого пола и потолка — у левого края вида (от ±0,000 объекта). Привязки — от левого чистового угла вида (облицовка стен вычтена), как на развёртках стен.
3. * — высота принята по практике монтажа: в данных прибора её нет; до разметки стен сверить по паспорту выбранного прибора (смеситель, инсталляция, сифон).
4. Стояки в помещении: Ст К1-1* Ø110, Ст В1-1* Ø32, Ст Т3-1* Ø32 — положение на плане выводов; выводы подключаются к ним по схеме разводки.
5. Ревизионные люки (стояки Ст К1-1*, Ст В1-1* (короб Ш1) 300×400): место в стене на развёртке не задано (записи реестра нет).
6. Часть подписей выводов не уместилась у знака: коды и высоты — в ведомости привязок.
7. Стены В: выводов В1, Т3, К1 нет — развёртка не строится (иначе лист-продолжение); приборы и проёмы этих стен — на плане выводов и развёртках стен чертёжника.
8. Расчёт систем водоснабжения и канализации и подбор оборудования выполняет проектная организация; лист задаёт места и высоты выводов.

1000 мм · печать 1:1

Изм.	Кол.уч	Лист	№ док.	Подп.	Дата
Разраб.		Кырлан А.С.			13.11.26
Пров.					
ГИП					
Н. контр.					
Утв.					

ГД-2026-003-АИ

Трёхкомнатная квартира

Общая площадь 78,95* м² · * размеры со скана, не замерены (реестр — л. 6–11, К-13)

Дизайн-проект интерьера трёхкомнатной квартиры

Стадия	Лист	Листов
РП	53	132

Развёртки мокрых зон: выводы ВК. Ванная

М 1:20


Кырлан Александр Сергеевич

выпуск 13.11.2026 № 6f3a8ab2c · стр. 58 из 157

Развёртки мокрых зон: выводы ВК. Кухня-гостиная

пом. 6 · выводы В1, Т3, К1 на стенах · высоты от чистого пола, привязки от чистовых углов, мм

Стена В (М 1:20)

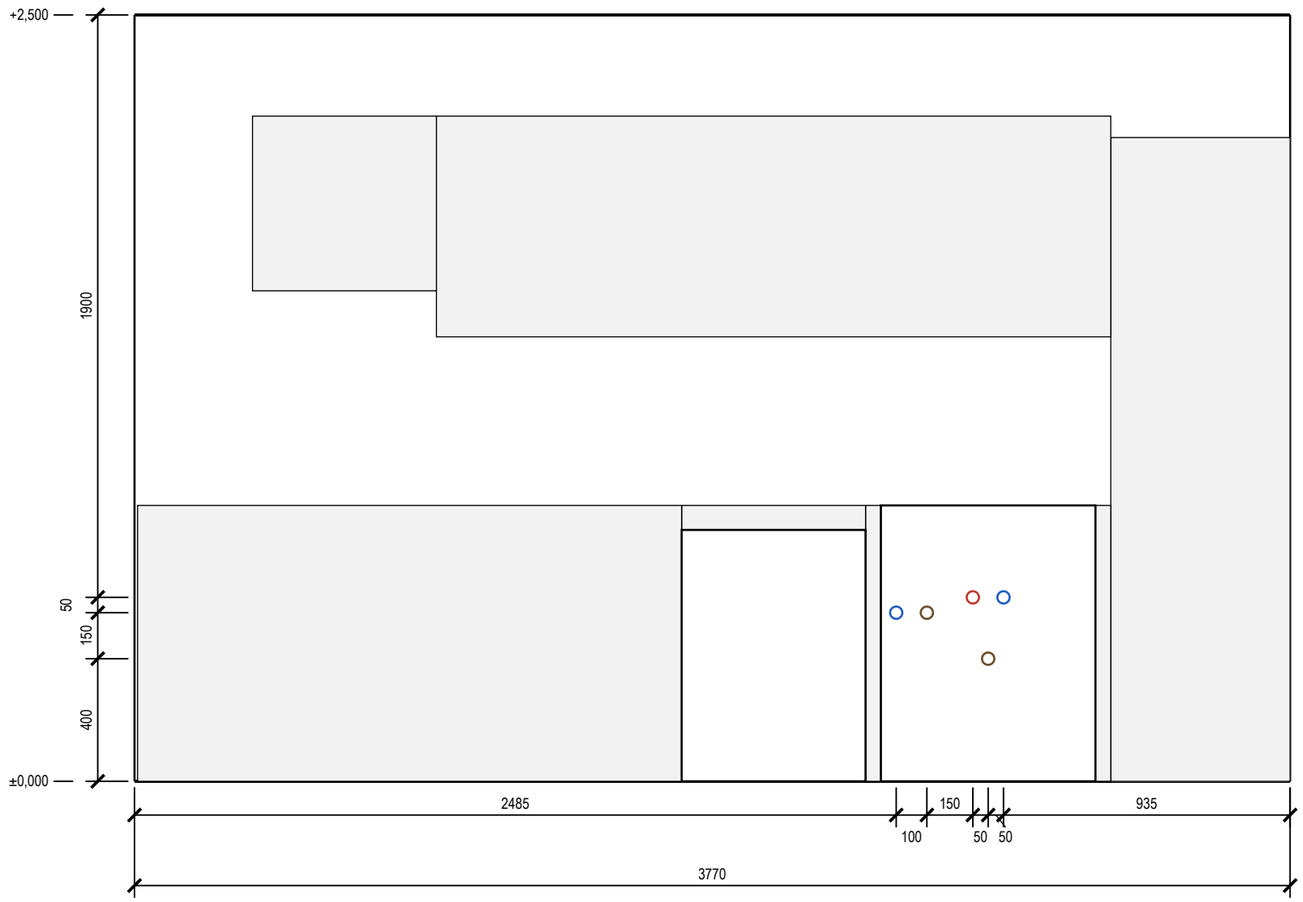

Допущения и предложения на листе

Основа листа: размеры сняты со скана плана заказчика по размерным цепочкам, контрольный обмер на объекте не выполнялся (К-13); высота потолка 2700 мм принята: на плане заказчика не указана (К-11); толщины стен приняты: наружные 250 мм, перегородки 150 мм (на плане 85–190 мм) (К-13); разрешённая мощность 15 кВт принята по типовой квартире, технических условий нет (К-14); утолщение стены 190 × 1360 мм и элемент 1470 × 160 мм плана заказчика не определены (К-12); ниши санузла 2 закрыты перегородкой и фальш-стеной: проектное решение, на плане заказчика ниша у входа открыта (К-18); несущие стены не определены: до технического заключения все существующие стены считаются несущими (К-20); окна существующие и сохраняются; подоконная доска и глубина откосов не заданы — приняты, не замерены (К-27); подрайон климата не задан — принят не северный (жилые от 2,5 м) (К-29).

Знак «*» — принято, не замерено и не подтверждено (замерить на объекте): К-8: П11 — Размер мойки — один источник: вырез в столешнице М7 на плане столешницы и в ведомости техники 700×480, в данных прибора было 500×450; П12.

См. лист открытых вопросов (лист 6, запись К-8; лист 7, записи К-11–К-14, К-18, К-20; лист 8, записи К-27, К-29).

Ведомость привязок выводов (от чистого пола и угла)

Код	Прибор	Ø	H, мм	Привязка, мм
В1-5	П11* мойка кухонная	½"	600	ст. В: 2835 от лев. угла
Т3-3	П11* мойка кухонная	½"	600	ст. В: 2735 от лев. угла
К1-5	П11* мойка кухонная	Ø50	400	ст. В: 2785 от лев. угла

Ведомость привязок (продолжение)

Код	Прибор	Ø	H, мм	Привязка, мм
В1-6	П12* посудомоечная машина	½"	550	ст. В: 2485 от лев. угла
К1-6	П12* посудомоечная машина	Ø40	550	ст. В: 2585 от лев. угла

Условные обозначения

- вывод В1 (код — в ведомости привязок)
- вывод Т3 (код — в ведомости привязок)
- вывод К1 (код — в ведомости привязок)
- сантехприбор по расстановке (габарит модели)
- дверной проём; окно — сплошной контур

Примечания

1. Габариты и высоты приборов, межосевые смесителей и места кранов — по паспортам выбранных приборов, сверяются до разметки стен.
2. Высоты H — от чистого пола помещения, мм; отметка чистого пола и потолка — у левого края вида (от ±0,000 объекта). Привязки — от левого чистового угла вида (облицовка стен вычтена), как на развёртках стен.
3. Ревизионные люки к арматуре и ревизиям в данных не заданы: место и размер не определены (записи реестра нет).
4. Мойка, ПММ и фильтр — выводы в шкафу мойки; диаметры и положение сифона и кранов сверить по паспортам приборов и чертежам модуля.
5. Часть подписей выводов не уместилась у знака: коды и высоты — в ведомости привязок.
6. Расчёт систем водоснабжения и канализации и подбор оборудования выполняет проектная организация; лист задаёт места и высоты выводов.

1000 мм · печать 1:1

Изм.	Кол.уч	Лист	№ док.	Подп.	Дата
Разраб.		Кырлан А.С.			13.11.26
Пров.					
ГИП					
Н. контр.					
Утв.					

ГД-2026-003-АИ

Трёхкомнатная квартира

Общая площадь 78,95* м² · * размеры со скана, не замерены (реестр — л. 6–11, К-13)

Дизайн-проект интерьера трёхкомнатной квартиры

Стадия	Лист	Листов
РП	54	132

Развёртки мокрых зон: выводы ВК. Кухня-гостиная

М 1:20

Кырлан Александр Сергеевич


выпуск 13.11.2026 № 6f3a8abb2c · стр. 59 из 157

Развёртки мокрых зон: выводы ВК. Санузел 2


ПРЕДВАРИТЕЛЬНО · не для производства работ · открыто пунктов: 28 (реестр — л. 6–11)

пом. 7 · выводы В1, Т3, К1 на стенах · высоты от чистого пола, привязки от чистовых углов, мм


Стена А (М 1:20)

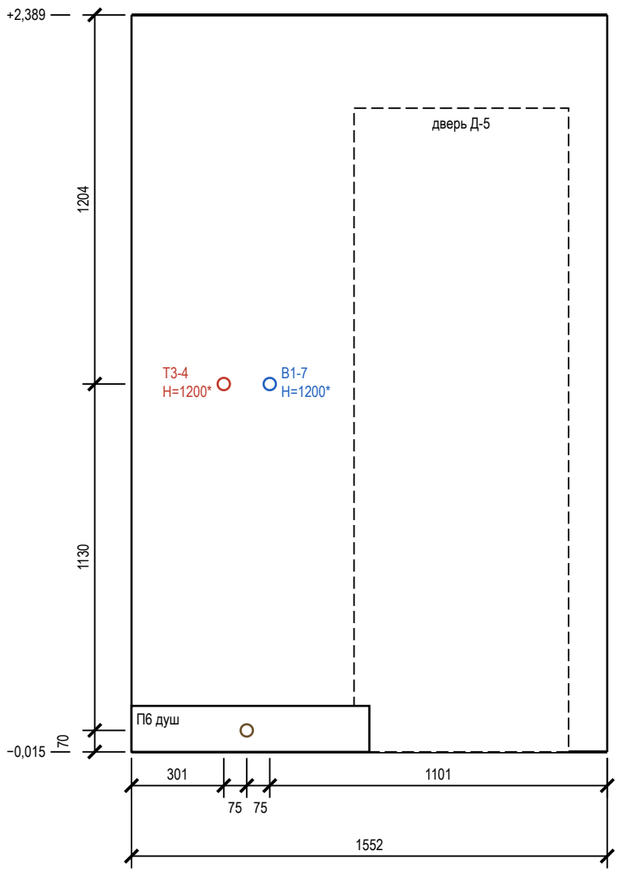


Стена Б (М 1:20)

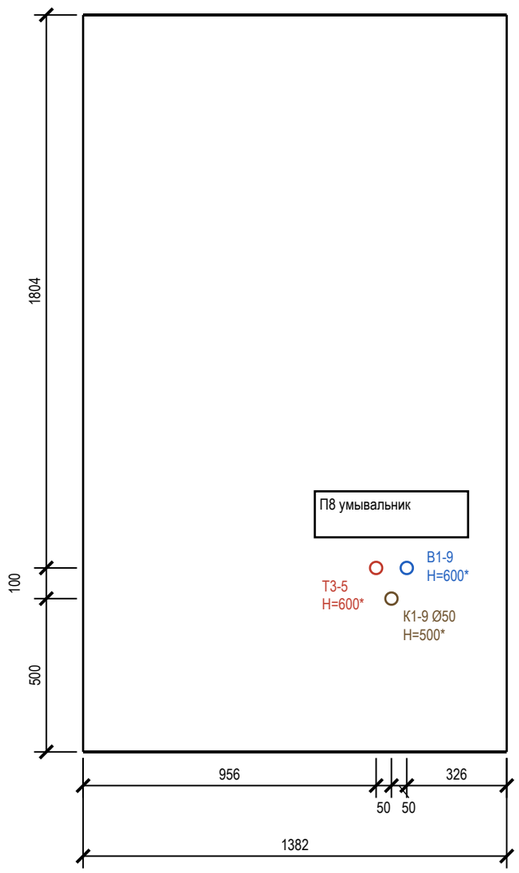

Стена В (М 1:20)

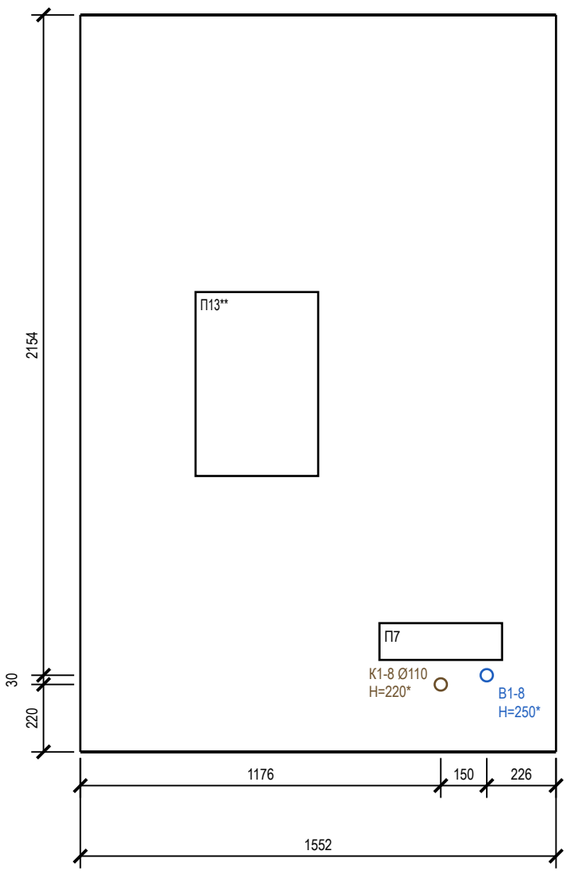

Стена Г (М 1:20)

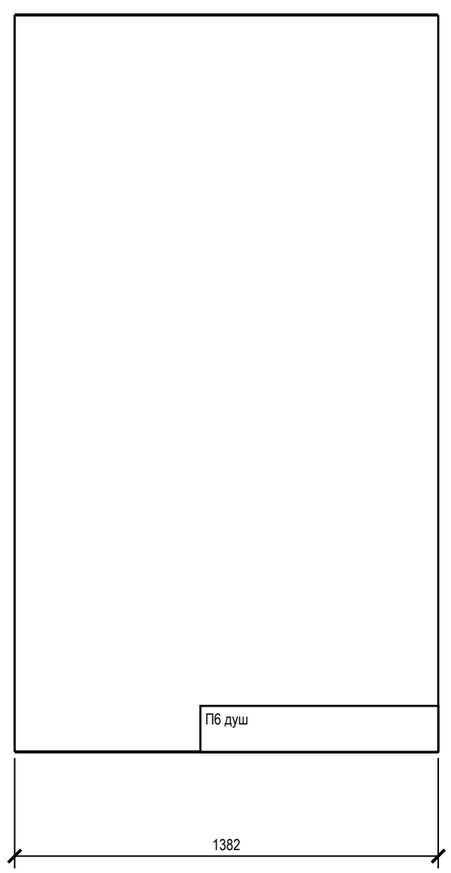

Ведомость привязок выводов (от чистого пола и угла)

Код	Прибор	Ø	H, мм	Привязка, мм
В1-7	П6 душ	½"	1200*	ст. А: 451 от лев. угла
Т3-4	П6 душ	½"	1200*	ст. А: 301 от лев. угла
К1-7	П6 душ	Ø50	70*	ст. А: 376 от лев. угла
В1-9	П8 умывальник	½"	600*	ст. Б: 1056 от лев. угла

Ведомость привязок (продолжение)

Код	Прибор	Ø	H, мм	Привязка, мм
Т3-5	П8 умывальник	½"	600*	ст. Б: 956 от лев. угла
К1-9	П8 умывальник	Ø50	500*	ст. Б: 1006 от лев. угла
В1-8	П7 унитаз подвесной	½"	250*	ст. В: 1326 от лев. угла
К1-8	П7 унитаз подвесной	Ø110	220*	ст. В: 1176 от лев. угла

Условные обозначения

- вывод В1 (код — в ведомости привязок)
- вывод Т3 (код — в ведомости привязок)
- вывод К1 (код — в ведомости привязок)
- сантехприбор по расстановке (габарит модели)
- дверной проём; окно — сплошной контур

Допущения и предложения на листе. Основа листа: размеры сняты со скана плана заказчика по размерным цепочкам, контрольный обмер на объекте не выполнялся (К-13); высота потолка 2700 мм принята: на плане заказчика не указана (К-11); толщины стен приняты: наружные 250 мм, перегородки 150 мм (на плане 85–190 мм) (К-13); разрешённая мощность 15 кВт принята по типовой квартире, технических условий нет (К-14); утолщение стены 190 × 1360 мм и элемент 1470 × 160 мм плана заказчика не определены (К-12); ниши санузла 2 закрыты перегородкой и фальш-стеной: проектное решение, на плане заказчика ниша у входа открыта (К-18); несущие стены не определены: до технического заключения все существующие стены считаются несущими (К-20); окна существующие и сохраняются; подоконная доска и глубина откосов не заданы — приняты, не замерены (К-27); подрайон климата не задан — принят не северный (жилые от 2,5 м) (К-29). Знак «*» — принято, не замерено (замерить). Знак «**» — предложено, не утверждено (согласовать). См. лист открытых вопросов (лист 7, записи К-11–К-14, К-17, К-18, К-20; лист 8, записи К-27, К-29; лист 9, запись ИЗ-1).

Примечания

1. Габариты и высоты приборов, межосевые смесителей и места кранов — по паспортам выбранных приборов, сверяются до разметки стен.
2. Высоты Н — от чистого пола помещения, мм; отметка чистого пола и потолка — у левого края вида (от ±0,000 объекта). Привязки — от левого чистового угла вида (облицовка стен вычтена), как на развёртках стен.
3. * — высота принята по практике монтажа: в данных прибора её нет; до разметки стен сверить по паспорту выбранного прибора (смеситель, инсталляция, сифон).
4. Стояки в помещении: Ст Т3-2* Ø32 — положение на плане выводов; выводы подключаются к ним по схеме разводки.
5. Ревизионные люки (стояки Ст К1-2*, Ст В1-2* (шахта Ш2) 300×400): место в стене на развёртке не задано (записи реестра нет).
6. Часть подписей выводов не уместилась у знака: коды и высоты — в ведомости привязок.
7. Расчёт систем водоснабжения и канализации и подбор оборудования выполняет проектная организация; лист задаёт места и высоты выводов.

1000 мм · печать 1:1

Изм.	Кол.уч	Лист	№ док.	Подп.	Дата
Разраб.		Кырлан А.С.			13.11.26
Пров.					
ГИП					
Н. контр.					
Утв.					

ГД-2026-003-АИ

Трёхкомнатная квартира

Общая площадь 78,95* м² · * размеры со скана, не замерены (реестр — л. 6–11, К-13)

Дизайн-проект интерьера трёхкомнатной квартиры

Стадия	Лист	Листов
РП	55	132

Развёртки мокрых зон: выводы ВК. Санузел 2

М 1:20

Кырлан Александр Сергеевич

выпуск 13.11.2026 № 6f3a8abb2c · стр. 60 из 157

Спецификация сантехнического оборудования

Форма 1 ГОСТ 21.110-2013 · ГД-2026-003-АИ-ВК.СО · приборы, арматура, трубопроводы

ПРЕДВАРИТЕЛЬНО · не для производства работ · открыто пунктов: 28 (реестр — л. 6–11)

Поз.	Наименование и техническая характеристика	Тип, марка, обозначение документа	Код продукции	Поставщик	Ед. изм.	Кол.	Масса 1 ед., кг	Примечание
	Санитарные приборы							
1	Ванна встраиваемая акриловая 1600×750 мм, с каркасом, экраном и отверстием слив-перелив	акриловая 1600×750, смеситель настенный		выбор заказчика	шт	1		П1
2	Унитаз подвесной безободковый, с сиденьем микролифт, крепёж и звукоизолирующая прокладка	аналог		выбор заказчика	шт	2		П2, П7
3	Инсталляция для подвесного унитаза: рама высотой 1120 мм, бачок, клавиша смыва (ось клавиши 1050 мм от чистого пола)	аналог		выбор заказчика	шт	2		П2, П7; короб ГКЛВ
4	Умывальник подвесной 450×600 мм, с отверстием под смеситель и переливом	аналог		выбор заказчика	шт	1		П3
5	Умывальник подвесной 350×500 мм, с отверстием под смеситель и переливом	аналог		выбор заказчика	шт	1		П8
6	Поддон душевой низкий 800×800 мм, с сифоном и выпуском Ø50, на ножках/подиуме	аналог		выбор заказчика	шт	1		П6
7	Мойка кухонная врезная 700×480 мм, с переливом	аналог		с кухонной мебелью	шт	1		П11*
8	Полотенцесушитель электрический, IP44, с терморегулятором	аналог		выбор заказчика	шт	2		П10**, П13**
	Смесители, сифоны и арматура приборов							
9	Смеситель для ванны настенный однорычажный, межосевое 150 мм, с душевым набором (лейка, шланг, держатель)	аналог		выбор заказчика	шт	1		П1
10	Смеситель для умывальника однорычажный, с донным клапаном	аналог		выбор заказчика	шт	2		П3, П8
11	Душевая система скрытого монтажа с термостатом: встраиваемая часть, верхний душ, ручная лейка	аналог		выбор заказчика	шт	1		П6; встраиваемая часть — до плитки
12	Смеситель кухонный однорычажный, высокий излив	аналог		выбор заказчика	шт	1		П11*
13	Обвязка ванны слив-перелив Ø40/50 с сифоном	аналог		выбор заказчика	шт	1		П1
14	Сифон для умывальника бутылочный Ø32/40–50, с гофрой к выпуску	аналог		выбор заказчика	шт	2		П3, П8
15	Сифон для мойки Ø40/50	аналог		выбор заказчика	шт	1		П11*
16	Сифон для посудомоечной машины с обратным клапаном, на выводе слива Ø40	аналог		выбор заказчика	шт	1		П12*
17	Сифон для стиральной машины встраиваемый в стену Ø50, с обратным клапаном	аналог		выбор заказчика	шт	1		П4*
18	Кран угловой ½"×½" с гибкой подводкой 40 см (умывальники, мойка)	аналог		выбор заказчика	шт	6		по 2 на прибор
19	Кран шаровой угловой ½"×¾" для подключения стиральной и посудомоечной машины	аналог		выбор заказчика	шт	2		П4*, П12*
	Трубопроводы							
20	Труба полипропиленовая PP-R PN20 Ø20×3,4 (В1)	ГОСТ 32415-2013		выбор заказчика	м	18,5	0,17	11,2 + 5,5 + 10 %
21	Труба PP-R, армированная стекловолокном, PN20 Ø20×2,8 (Т3)	ГОСТ 32415-2013		выбор заказчика	м	13,5	0,15	8,2 + 3,8 + 10 %
22	Труба канализационная ПП Ø40 (К1)	ГОСТ 32414-2013		выбор заказчика	м	1		0,3 + 0,6 + 10 %
23	Труба канализационная ПП Ø50 (К1)	ГОСТ 32414-2013		выбор заказчика	м	11		7,7 + 2,1 + 10 %
24	Труба канализационная ПП Ø110 (К1)	ГОСТ 32414-2013		выбор заказчика	м	4		2,9 + 0,4 + 10 %
	Фасонные части и выводы							
25	Отвод канализационный ПП 45° Ø40	ГОСТ 32414-2013		выбор заказчика	шт	2		2 шт. на поворот
26	Отвод канализационный ПП 45° Ø50	ГОСТ 32414-2013		выбор заказчика	шт	20		2 шт. на поворот
27	Отвод канализационный ПП 45° Ø110	ГОСТ 32414-2013		выбор заказчика	шт	10		2 шт. на поворот
28	Тройник канализационный ПП 45° (врезки ветвей)	ГОСТ 32414-2013		выбор заказчика	шт	8		
29	Ревизия канализационная ПП (после поворота трассы)	ГОСТ 32414-2013		выбор заказчика	шт	9		доступ сохранить
30	Фитинги PP-R Ø20: тройники, угольники 90° (ветви и повороты В1, Т3)	ГОСТ 32415-2013		выбор заказчика	шт	34		
31	Водорозетка PP-R Ø20×½" настенная, с креплением	ГОСТ 32415-2013		выбор заказчика	шт	14		коды — лист выводов
	Узлы ввода, люки, короба							
32	Кран шаровой латунный Ду15 PN16 (отключение ввода)	аналог		выбор заказчика	шт	4		Ст В1-1*, Ст В1-2*, Ст Т3-1*, Ст Т3-2*
33	Фильтр сетчатый косой Ду15	аналог		выбор заказчика	шт	4		
34	Счётчик воды крыльчатый Ду15 (ХВ, ГВ), с поверкой	аналог		выбор заказчика	шт	4		пломба УК
35	Клапан обратный Ду15	аналог		выбор заказчика	шт	4		
36	Люк ревизионный нажимной под плитку 300×400 мм	аналог		выбор заказчика	шт	2		к стоякам и арматуре
37	Звукоизоляция стояка К1 в коробе: рулонный звукоизоляционный материал ≥ 10 мм, обмотка стояка на высоту этажа	аналог		выбор заказчика	м	5,4		Ст К1-1*, Ст К1-2*
38	Короб К1 над полом: профиль ПН/ПС, ГКЛВ 12,5 мм под плитку	аналог		выбор заказчика	м	2,4		сечение — лист разводки

Примечания

1. Форма 1 ГОСТ 21.110-2013, ширины граф изменены по п. 4.1. «Аналог» — аналог по характеристикам: модели внести до черновых работ, привязки выводов сверить по паспортам.
2. Бытовая техника не входит (показана арматура подключения), мойка — в комплекте кухни (марка — модуля кухни, как у столяра). Длины труб — трасса листа разводки + подъёмы + 10 %.
3. Стояк К1 в коробе — звукоизоляция стояка в коробе без жёсткого контакта короба с трубой. Стояки со «*» (Ст К1-1*, Ст В1-1*, Ст К1-2*, Ст В1-2*, Ст Т3-1, Ст Т3-2) приняты — положение и число узлов ввода сверить на объекте.
4. Расчёт систем водоснабжения и канализации, диаметры магистралей и подбор оборудования выполняет проектная организация.
5. Допущение проекта: санузел 2 — проектное решение: ниша 1600 × 1840 у входа (на плане открыта в кухню-гостиную) закрыта перегородкой по линии низа прихожей; ниша 660 × 260 у наружной стены (уступ по плану) закрыта фальш-стеной по линии уступа, в ней рама инсталляции унитаза.
6. Допущение проекта: стояки: у ванной — в коробе Ш1 248 × 459; у санузла 2 — в стене-пилоне 270 мм (Ш2) между санузлом 2 и кухней; люки 300 × 400; положение стояков условно — сверить на объекте.
7. Допущение проекта: кухня: раскладка гарнитура принята проектной, решение автора (ИЗ-12) — мойка М7* у шахты Ш2, ПММ М14* рядом с мойкой, варочная и духовой шкаф в М8*, вытяжка М15**, холодильник М6**; выводы техники — по типовой расстановке; условие: до начала черновых работ сверить раскладку и выводы с чертежом кухни от изготовителя, выводы пересматриваются по его чертежу (вопрос К-8).
8. Допущение проекта: стиральная машина П4* — вертикальной загрузки, габарит в плане 400 × 600 мм (ширина 400 вдоль стены Б): условие закупки, а не пожелание, решение автора (ИЗ-11); машина с фронтальной загрузкой или большего габарита не подходит — перед люком ванна П1; модель не выбрана, габарит и подводку сверить по паспорту до закрытия трасс (вопрос К-19).
9. Марки из допущений, которых нет на этом листе: М6**, М7*, М8*, М14*, М15** — лист 77.

Допущения и предложения на листе. Основа листа: размеры сняты со скана плана заказчика по размерным цепочкам, контрольный обмер на объекте не выполнялся (К-13); высота потолка 2700 мм принята: на плане заказчика не указана (К-11); толщины стен приняты: наружные 250 мм, перегородки 150 мм (на плане 85–190 мм) (К-13); разрешённая мощность 15 кВт принята по типовой квартире, технических условий нет (К-14); утолщение стены 190 × 1360 мм и элемент 1470 × 160 мм плана заказчика не определены (К-12); ниши санузла 2 закрыты перегородкой и фальш-стеной: проектное решение, на плане заказчика ниша у входа открыта (К-18); несущие стены не определены: до технического заключения все существующие стены считаются несущими (К-20); окна существующие и сохраняются; подоконная доска и глубина откосов не заданы — приняты, не замерены (К-27); подрайон климата не задан — принят не северный (жилые от 2,5 м) (К-29). Знак «*» — принято, не замерено (замерить): ИЗ-11, К-19: П4; К-8: М8, П11. Знак «**» — предложено, не утверждено (согласовать). См. лист открытых вопросов (лист 6, запись К-8; лист 7, записи К-11–К-14, К-17–К-20; лист 8, записи К-27, К-29; лист 9, записи ИЗ-1, ИЗ-5; лист 10, запись ИЗ-11).

Изм.	Кол.уч	Лист	№ док.	Подп.	Дата	ГД-2026-003-АИ			
						Трёхкомнатная квартира Общая площадь 78,95* м² · * размеры со скана, не замерены (реестр — л. 6–11, К-13)			
Разраб.		Кырлан А.С.			13.11.26	Дизайн-проект интерьера трёхкомнатной квартиры	Стадия	Лист	Листов
Пров.							РП	56	132
ГИП									
Н. контр.						Спецификация сантехнического оборудования М б/м	Кырлан Александр Сергеевич		
Утв.									

выпуск 13.11.2026 № 6f3a8abb2c · стр. 61 из 157

Техническое задание на подбор светильников

Параметры для подбора: светильники, ленты и блоки питания, слои света, сценарии помещений со светорегуляторами · б/м

Параметры светильников для подбора

Поз.	Марки	Наименование	Установка	Кол.	P, Вт	Σ P, Вт	Ф, лм	Тц, К	Ra	Угол, °	IP	Дим.	Слой	Группа	Пом.
1	Св1–Св8	Встраиваемый точечный	в ГКЛ, корпус ≤ 70 мм	8	12	96	1000	2700	90	—	20	—	общий	L1	1
2	Св9	Лента светодиодная 24 В	в карнизе короба, профиль с рассеивателем	15,5 м	9,6/м	148,8	900/м	2700	90	—	20	да	акцентный	L2	1
3	Св10, Св11, Св24, Св25	Настенный (бра)	на стене, H=1500	4	6	24	400	2700	90	60	20	—	рабочий	L3, L9	1, 4
4	Св12–Св14, Св51	Встраиваемый точечный	в ГКЛ, корпус ≤ 70 мм	4	6	24	500	3000	90	—	44	—	общий	L4, L17	2, 7
5	Св15**, Св52**	Настенный светильник над зеркалом, драйвер встроен	над зеркалом, H=1900	2	8	16	600	3000	90	—	44	—	рабочий	L5, L18	2, 7
6	Св16	Потолочный накладной	на потолке, засветка стены	1	10	10	900	3000	90	—	20	—	общий	L6	3
7	Св17–Св22	Встраиваемый точечный	в ГКЛ, корпус ≤ 70 мм	6	12	72	1050	2700	90	—	20	—	общий	L7	4
8	Св23	Лента светодиодная 24 В	в карнизе короба, профиль с рассеивателем	12,3 м	9,6/м	118,5	900/м	2700	90	—	20	да	акцентный	L8	4
9	Св26–Св29, Св53, Св54	Встраиваемый точечный	в ГКЛ, корпус ≤ 70 мм	6	7	42	600	3000	90	—	20	—	общий	L10	5, 8
10	Св30**	Лента светодиодная 24 В	на поверхности, профиль с рассеивателем, датчик движения	1,8 м	4,8/м	8,6	150/м	2700	90	—	20	нет	ночной	L11	5
11	Св31**, Св32**, Св33**, Св34**, Св35**, Св36**, Св37**, Св38**, Св39**, Св40**	Встраиваемый точечный	в ГКЛ, корпус ≤ 70 мм	10	12	120	1000	3000	90	—	20	да	общий	L12	6
12	Св41	Лента светодиодная 24 В	в карнизе короба, профиль с рассеивателем	22,1 м	9,6/м	211,8	900/м	2700	90	—	20	да	акцентный	L13	6
13	Св42**, Св43**, Св44**	Подвесной	подвес, низ H=1450	3	9	27	800	3000	90	—	20	да	общий	L14	6
14	Св45–Св48	Встраиваемый точечный	в ГКЛ, корпус ≤ 70 мм	4	10	40	900	3000	90	—	20	—	общий	L15	6
15	Св49**	Линейный настенный	под верхними шкафами, H=1440	1	18	18	1500	3000	90	—	20	да	рабочий	L16	6
16	Св50	Встраиваемый точечный	в ГКЛ, корпус ≤ 70 мм	1	7	7	600	3000	90	—	44	—	общий	L17	7
		Итого		**50 шт + 51,7 м**		**983,7**									

LED-ленты, линейные светильники и блоки питания

Марка	Пом.	L, м	U, В	Вт/м	Σ P, Вт	БП	P БП, Вт	Загр., %	Питание	Доступ к БП
Св9	1	15,5	24	9,6	148,8	БП1	200	74	с двух концов	люк 300×300 в коробе потолка ПТ1
Св23	4	12,3	24	9,6	118,5	БП2	200	59	с двух концов	люк 300×300 в коробе потолка ПТ1
Св30**	5	1,8	24	4,8	8,6	БП3	20	43	с одного конца	в шкафу М16, верхняя полка
Св41	6	22,1	24	9,6	211,8	БП4	300	71	с двух концов	люк 300×300 в коробе потолка ПТ1
Св49**	6	3	24	—	18	БП5**	60	30	встроенный ввод	в пенале М6**, верх, съёмная панель

Сценарии (помещения со светорегуляторами)

Помещение	Сценарий	Горят группы (уровень)	Управление
6. Кухня-гостиная	Вечер	L12 споты гостиной — 30 %; L13 подсветка короба — 100 %; L14 подвесы над столом — 50 %; остальные выкл.	светорегуляторы S10, S11**, S17**
	Ужин	L13 подсветка короба — 60 %; L14 подвесы над столом — 100 %; L16 подсветка столешницы — 30 %; остальные выкл.	светорегуляторы S11**, S12**, S17**
	Кино	L13 подсветка короба — 20 %; остальные выкл.	светорегулятор S17**
	Готовка	L12 споты гостиной — 50 %; L15 споты кухни — вкл.; L16 подсветка столешницы — 100 %; остальные выкл.	светорегуляторы S10, S12**; выключатель S18**

Слои света по помещениям

Пом.	Помещение	Слои света — группы	Σ P, Вт
1	Спальня 1	общий — L1; рабочий — L3; акцентный — L2	256,8
2	Ванная	общий — L4; рабочий — L5	26
3	Гардеробная	общий — L6	10
4	Спальня 2	общий — L7; рабочий — L9; акцентный — L8	202,5
5	Прихожая	общий — L10; ночной — L11	36,6
6	Кухня-гостиная	общий — L12, L14, L15; рабочий — L16; акцентный — L13	416,8
7	Санузел 2	общий — L17; рабочий — L18	21
8	Коридор	общий — L10	14

Слои света

общий — равномерный свет помещения, по норме освещённости

рабочий — местный свет задачи: столешница, зеркало, чтение у кровати

акцентный — подсветка потолка, стен и ниш; не входит в поток общего света

ночной — путь спальня → санузел: не выше 2700 К, малая яркость, датчик движения

Допущения и предложения на листе

Основа листа: размеры сняты со скана плана заказчика по размерным цепочкам, контрольный обмер на объекте не выполнялся (К-13); высота потолка 2700 мм принята: на плане заказчика не указана (К-11); толщины стен приняты: наружные 250 мм, перегородки 150 мм (на плане 85–190 мм) (К-13); разрешённая мощность 15 кВт принята по типовой квартире, технических условий нет (К-14); утолщение стены 190 × 1360 мм и элемент 1470 × 160 мм плана заказчика не определены (К-12); ниши санузла 2 закрыты перегородкой и фальш-стеной: проектное решение, на плане заказчика ниша у входа открыта (К-18); несущие стены не определены: до технического заключения все существующие стены считаются несущими (К-20); окна существующие и сохраняются; подоконная доска и глубина откосов не заданы — приняты, не замерены (К-27); подрайон климата не задан — принят не северный (жилые от 2,5 м) (К-29).

Знак «**» — предложение проектировщика, заказчиком не утверждено (согласовать с заказчиком): Св15 — Сдвиг под раскладку плитки стены Г на 137 мм вдоль стены — ось на шве или в центре плитки, привязка по таблице листа; Св30 — открытая лента в накладном профиле вместо «в коробе»: короба в потолке нет — подвесной потолок помещения без короба и ниши LED; S17 — свой пост группе L13: сценарии «Вечер», «Ужин», «Кино», «Готовка» включают её отдельно от L12 — на одном светорегуляторе не набрать; S18 — свой пост группе L15: сценарии «Вечер», «Ужин», «Готовка» включают её отдельно от L14 — на одном светорегуляторе не набрать; Св31, Св32, Св33, Св34, Св35, Св36, Св37, Св38, Св39, Св40 — ряды — по зоне гостиной (по мебели); Св52 — Сдвиг под раскладку плитки стены Б на 14 мм вдоль стены — ось на шве или в центре плитки, привязка по таблице листа; ИЗ-3: S11, S12 — светорегулятор добавлен разработчиком проекта; Св42, Св43, Св44, Св49, БП5 — диммируемость добавлена разработчиком проекта под светорегуляторы S11 и S12; ИЗ-5, К-8: М6.

См. лист открытых вопросов (лист 6, запись К-8; лист 7, записи К-11–К-14, К-18, К-20; лист 8, записи К-27, К-29; лист 9, записи ИЗ-3, ИЗ-5).

Примечания

1. Позиции и марки Св — те же, что на плане освещения (лист 38) и в ведомости светильников (лист 40); группы L — по плану выключателей (лист 39).
2. Модели светильников не выбраны: лист — техническое задание на подбор. Модель по строке таблицы: поток, Тц, Ra, угол, IP и регулировка яркости не хуже указанных, мощность не больше; встраиваемые — под глубину короба (графа «Установка»). IP 20 — сухие помещения. После выбора моделей (артикул, производитель) лист выпускается как «Спецификация светильников».
3. Длина LED-ленты в карнизе — по линии карниза плана потолков (лист 59); Σ P = Вт/м × длина. Блок питания загружен не больше чем на 80 %; лента 24 В длиннее 10 м питается с двух концов; доступ к блоку питания — люк ревизии 300×300 мм или место, указанное в таблице.
4. Сценарии: % — яркость группы на светорегуляторе; «вкл.» — группа на обычной клавише; группы, не названные в строке, выключены. Светильники и блоки питания групп на светорегуляторе — с регулировкой яркости. Клавиши и светорегуляторы — лист 39.
5. В пом. 1, 4 свет включается клавишами групп — лист 39. Общий сценарий «Ушёл» без системы управления светом не выполняется: группы включают и выключают клавишами.
6. Мощность и поток в таблице — требования к подбору (поток не меньше, мощность не больше указанных); после выбора модели — по её паспорту, Σ P — установленная мощность освещения. Оценка освещённости — на плане освещения; это не светотехнический расчёт.

Изм.	Кол.уч	Лист	№ док.	Подп.	Дата
Разраб.		Кырлан А.С.			13.11.26
Пров.					
ГИП					
Н. контр.					
Утв.					

ГД-2026-003-АИ

Трёхкомнатная квартира

Общая площадь 78,95* м² · * размеры со скана, не замерены (реестр — л. 6–11, К-13)


Дизайн-проект интерьера трёхкомнатной квартиры	Стадия	Лист	Листов
	РП	57	132
Техническое задание на подбор светильников М б/м	**Кырлан Александр Сергеевич**		

выпуск 13.11.2026 № 6f3a8abb2c · стр. 62 из 157

Схема каркаса перегородки П-1

С112; вид, сечения и узлы: каркас, обрамление проёма и примыкания


Вид на каркас без обшивки (М 1:20)

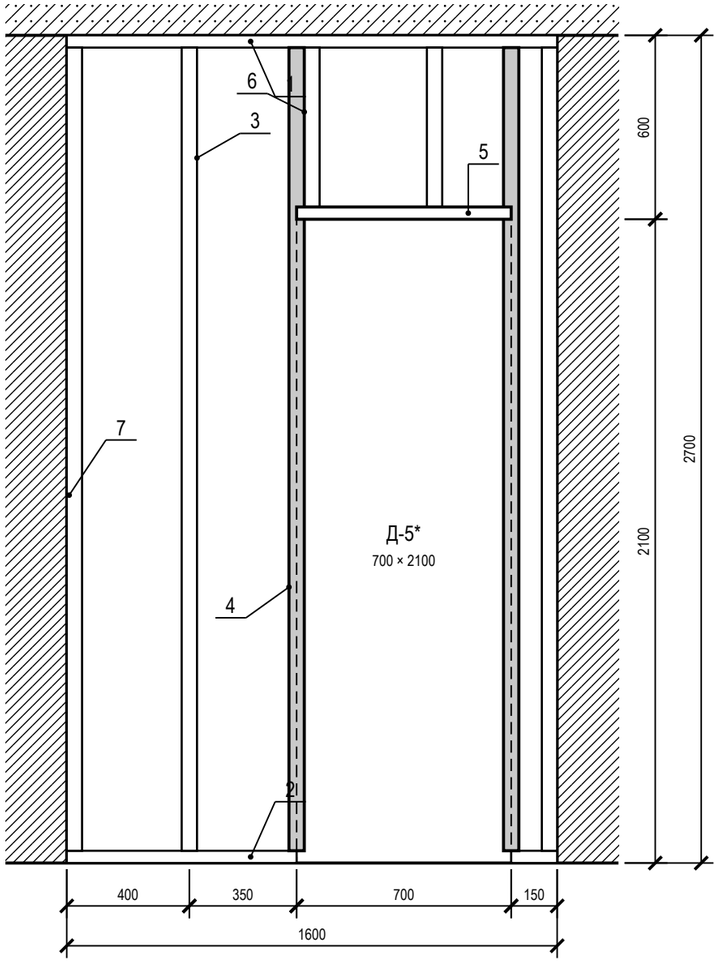

Оси — стойки каркаса; полки профиля на виде условны

Сечение А–А по стойке (М 1:5)


сверху — пом. 6, окраска

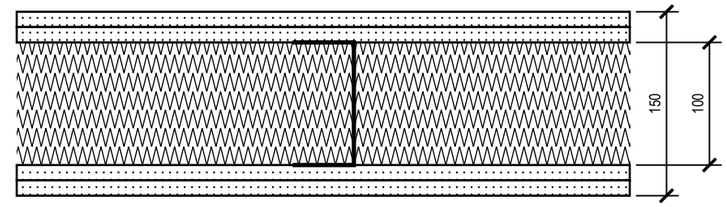

снизу — пом. 7, плитка


поз. 9 — ГКЛВ 12,5 мм в 2 слоя с каждой стороны; поз. 3 — ПС 100; поз. 8 — минвата 100 мм (принято)

Сечение Б–Б у проёма, на уровне ниже перемычки (М 1:5)

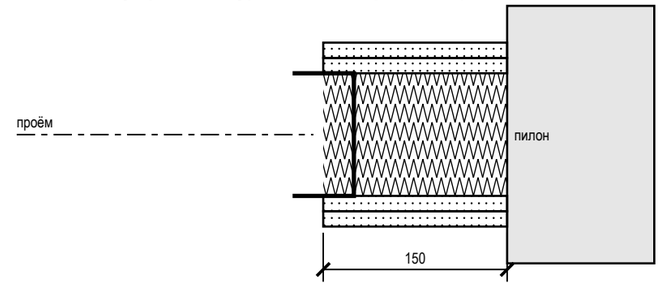


поз. 4 — УА 100, обрамление проёма; обшивка по краю проёма, простенок 150 мм до пилона

Узел 1. К плите (М 1:5)

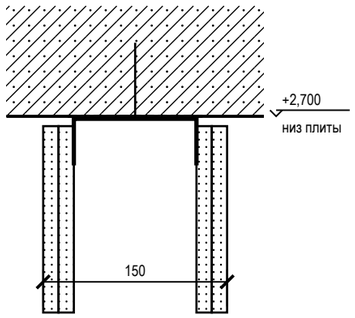

Узел 2. К полу (М 1:5)

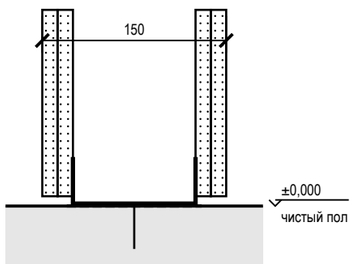

Ведомость элементов каркаса

Поз.	Наименование	Кол-во	Ед.
1	ПН 100 по потолку (к перекрытию)	1,60	м
2	ПН 100 по полу, без проёма	0,90	м
3	ПС 100 через 400 мм	3 × 2,70	м
4	УА 100 по краям проёма	2 × 2,70	м
5	ПН 100 перемычка над проёмом	0,70	м
6	ПС 100 над перемычкой	2 × 0,60	м
7	Лента уплотнительная под профили	7,90	м
8	Минвата в полость, 100 мм	2,85	м²
9	ГКЛВ 12,5 мм, 2 слоя с двух сторон	11,40	м²

Итого: ПН 3,20 м, ПС 9,30 м, УА 5,40 м; сторона 2,85 м²

Примечания

1. П-1** (С112, ГКЛВ в 2 слоя с каждой стороны, толщина 150 мм, высота 2700 мм до плиты) — предложение проектировщика, автором не утверждено (К-18, К-4); ось и длина 1600 мм — со скана плана заказчика (контрольный обмер не выполнялся).
2. Шаг стоек 400 мм — по данным (под плитку и во влажной зоне). Размеры сечений профилей — «ПС 100», «УА 100» по данным и каталогу; толщины листов — ГОСТ 32614-2012.
3. Принято: проём Д-5 в каркасе 700 × 2100 мм принят по размеру полотна: короб скрытой двери (модель, размеры) не выбран — проём пересчитать по коробке до монтажа УА (К-18, К-4, К-25).
4. Принято: перемычка над проёмом — направляющий профиль по верху проёма на всю его ширину; короткие стойки ПС над перемычкой на шаге каркаса: по практике узла Knauf, не по данным объекта (К-18, К-4).
5. Принято: заполнение полости — минераловатная плита на всю глубину профиля (Rw системы С112 нормируют с заполнением); марка и плотность выбираются при закупке (К-18, К-4).
6. Принято: длина стойки равна высоте перегородки: стойки режут на высоту между направляющими при монтаже, зазоры до плиты и пола в проекте не заданы.
7. Обшивку крепят к стойкам шурупами через слой, швы слоёв вразбежку; зазоры обшивки до плиты и пола, шаг дюбелей, марка заполнения — по ТУ системы и узлу изготовителя.

Допущения и предложения на листе

Основа листа: размеры сняты со скана плана заказчика по размерным цепочкам, контрольный обмер на объекте не выполнялся (К-13); высота потолка 2700 мм принята: на плане заказчика не указана (К-11); толщины стен приняты: наружные 250 мм, перегородки 150 мм (на плане 85–190 мм) (К-13); разрешённая мощность 15 кВт принята по типовой квартире, технических условий нет (К-14); утолщение стены 190 × 1360 мм и элемент 1470 × 160 мм плана заказчика не определены (К-12); ниши санузла 2 закрыты перегородкой и фальш-стеной: проектное решение, на плане заказчика ниша у входа открыта (К-18); несущие стены не определены: до технического заключения все существующие стены считаются несущими (К-20); окна существующие и сохраняются; подоконная доска и глубина откосов не заданы — приняты, не замерены (К-27); подрайон климата не задан — принят не северный (жилые от 2,5 м) (К-29).

Знак «**» — предложение проектировщика, заказчиком не утверждено (согласовать с заказчиком): К-4, К-18: П-1 — проектное решение исполнителя: на плане заказчика ниша у входа открыта в кухню-гостиную; конструкция не утверждена автором (вопрос К-18), положение и размеры сняты со скана (К-13).

См. лист открытых вопросов (лист 6, запись К-4; лист 7, записи К-11–К-14, К-18, К-20; лист 8, записи К-27, К-29).

Изм.	Кол.уч	Лист	№ док.	Подп.	Дата
Разраб.		Кырлан А.С.			13.11.26
Пров.					
ГИП					
Н. контр.					
Утв.					

ГД-2026-003-АИ

Трёхкомнатная квартира

Общая площадь 78,95* м² · * размеры со скана, не замерены (реестр — л. 6–11, К-13)

Дизайн-проект интерьера трёхкомнатной квартиры	Стадия	Лист	Листов
	РП	58	132

Схема каркаса перегородки П-1

М 1:20; 1:5

Кырлан Александр Сергеевич

выпуск 13.11.2026 № 6f3a8abb2c · стр. 63 из 157

06


Потолки и ГКЛ-конструкции

Кырлан Александр Сергеевич

выпуск 13.11.2026 · 6f3a8abb2c · стр. 64 из 157

План потолков

Уровни и марки потолков, короба с подсветкой, ниши под шторы, люки, вырезы · отметки низа от ±0,000 чистого пола · размеры в мм

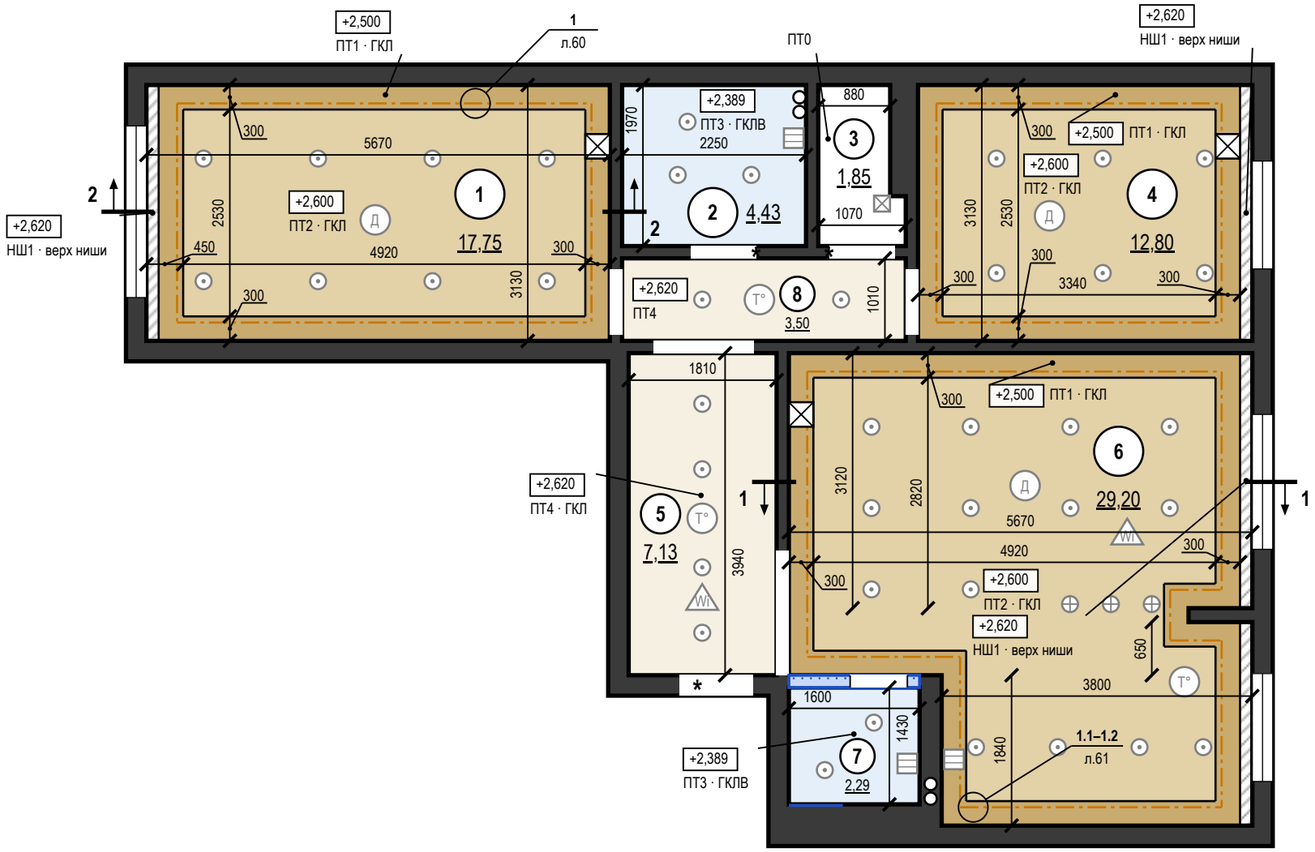

Ведомость потолков

Пом.	Марка	Конструкция	Низ / верх ниши	S, м²	Q
1	ПТ1	ГКЛ П113, короб LED	+2,500	4,83	Q3
1	ПТ2	ГКЛ П113	+2,600	12,45	Q3
1	НШ1	ниша под шторы 150×120	+2,620	0,47	
2	ПТ3	ГКЛВ П113	+2,389	4,43	Q3
3	ПТ0	Существующий потолок, окраска	+2,700	1,85	
4	ПТ1	ГКЛ П113, короб LED	+2,500	3,88	Q3
4	ПТ2	ГКЛ П113	+2,600	8,45	Q3
4	НШ1	ниша под шторы 150×120	+2,620	0,47	
5	ПТ4	ГКЛ П113	+2,620	7,13	Q3
6	ПТ1	ГКЛ П113, короб LED	+2,500	6,80	Q3
6	ПТ2	ГКЛ П113	+2,600	21,56	Q3
6	НШ1	ниша под шторы 150×120	+2,620	0,84	
7	ПТ3	ГКЛВ П113	+2,389	2,29	Q3
8	ПТ4	ГКЛ П113	+2,620	3,50	Q3
		Итого		**78,95**	

Условные обозначения

- ПТ1 — ГКЛ по каркасу П113, низ +2,500, пояс-короб с карнизом LED
- ПТ2 — ГКЛ по каркасу П113, низ +2,600
- ПТ3 — ГКЛВ по каркасу П113, низ +2,389
- ПТ4 — ГКЛ по каркасу П113, низ +2,620
- ПТ0 — существующий потолок, окраска, без подвесного потолка, низ +2,700
- НШ1 — ниша под шторы 150×120, верх +2,620
- граница уровней потолка (перепад)
- LED-лента в нише подсветки (карниз короба, ниша фигуры)
- стояк: К1 — канализация, В1 — ХВС, Т3 — ГВС
- люк ревизии в потолке 300×300 мм (доступ к БП LED)
- светильник встраиваемый — подложка с плана освещения
- светильник накладной — подложка с плана освещения
- светильник подвесной — подложка с плана освещения
- Д — извещатель дымовой на потолке — подложка
- T° — извещатель тепловой на потолке — подложка
- Wi — точка доступа Wi-Fi на потолке — подложка
- решётка вытяжки в потолке — подложка с плана вентиляции
- линия разреза у стен помещения, стрелка — направление взгляда
- место узла и сечений М 1:10: номер узла или сечений на полке, под полкой лист

Условные обозначения (продолжение)

- +2,600 — отметка низа потолка, м (у ниши под шторы — верх ниши); под ней марка потолка
- новое — возводится по проекту (синим)
- 1 — номер помещения, площадь м²

Допущения и предложения на листе. Основа листа: размеры сняты со скана плана заказчика по размерным цепочкам, контрольный обмер на объекте не выполнялся (К-13); высота потолка 2700 мм принята: на плане заказчика не указана (К-11); толщины стен приняты: наружные 250 мм, перегородки 150 мм (на плане 85–190 мм) (К-13); разрешённая мощность 15 кВт принята по типовой квартире, технических условий нет (К-14); утолщение стены 190 × 1360 мм и элемент 1470 × 160 мм плана заказчика не определены (К-12); ниши санузла 2 закрыты перегородкой и фальш-стеной: проектное решение, на плане заказчика ниша у входа открыта (К-18); несущие стены не определены: до технического заключения все существующие стены считаются несущими (К-20); окна существующие и сохраняются; подоконная доска и глубина откосов не заданы — приняты, не замерены (К-27); подрайон климата не задан — принят не северный (жилые от 2,5 м) (К-29). Знак «*» — принято, не замерено (замерить): К-17: Ст К1-1, Ст В1-1, Ст К1-2, Ст В1-2. Знак «**» — предложено, не утверждено (согласовать): К-4, К-18: П-1; К-18: П-2; К-25: дверь пом. 6 (стена В). См. лист открытых вопросов (лист 6, запись К-4; лист 7, записи К-11–К-14, К-17, К-18, К-20; лист 8, записи К-25–К-27, К-29).

Примечания

1. За отметку ±0,000 принят уровень чистого пола сухих помещений (готовое покрытие), а не существующего пола; пол пом. 2, 7 — −0,015; верх плиты перекрытия −0,064 — расчётный по пирогу пола, не замерен; существующий пол снимается до плиты, его отметка не замерена. Отметки в прямоугольниках — низ потолка; низ перекрытия +2,700. Марка потолка — одна конструкция и отметка на весь альбом.
2. Размеры помещений в свету (ширина × длина, мм), не поместившиеся на плане: пом. 3 — 880 × 1360, 1070 × 610; пом. 4 — 4090 × 3130; пом. 6 — 5670 × 3120, 4890 × 170, 5670 × 650, 3800 × 1840; пом. 8 — 3470 × 1010.
3. Потолки ГКЛ — каркасная система П113: подвесы через 1000 (с запасом: СП 163, табл. 14 — до 1100 при 0,15 кН/м²), несущие профили через 500, основные через 1200 мм; листы — поперёк несущих профилей. В помещениях 2, 7 — ГКЛВ на оцинкованном каркасе.
4. Нижний уровень — пояс-короб по периметру шириной 300 мм (карниз подсветки + 150 мм полки), верхний — поле внутри пояса: пом. 1, 4, 6.
5. LED-лента в алюминиевом профиле посередине карниза короба шириной 300 мм (узел 1, лист 60); длина по плану: пом. 1 — 15,5 м (в плане освещения 15,5); пом. 4 — 12,3 м (в плане освещения 12,3); пом. 6 — 22,1 м (в плане освещения 22,1).
6. Ниши под шторы 150×120 мм — на всю длину стены с окном; карниз — на закладной до обшивки (узел 2, лист 60).
7. Примыкание к стенам: теневой шов 15 мм, техзазор 3 мм — пом. 1, 4, 6, по стенам, выровненным штукатуркой (узел 1); пом. 2, 5, 7, 8 — разделительная лента.
8. Светильники и потолочные устройства — подложка с планов освещения, слаботочных систем и вентиляции (положение — по ним); вырезы и закладные — по ведомости на листе, до обшивки; отверстия не совмещать с профилями, глубина корпуса светильника до 70 мм.
9. Разрезы 1–1, 2–2 — на листе 60; высоты мебели и дверных блоков сверены с низом потолка в разрезах.
10. Узлы по выноскам на плане: узлы 1, 2 — лист 60; сечения М 1:10 по помещениям — лист 61.
11. Шпаклевание ГКЛ и условия приёмки — Q3: рассеянный дневной свет, осмотр с 2 м; боковой свет не оценивается.
12. Ведомость вырезов и закладных в потолке — на листе 60; вырезы и закладные — до обшивки.
13. Люки ревизии 300×300 мм — по центру блоков питания LED (БП1, БП2, БП4; координаты — план освещения).
14. Сечения потолков М 1:10: пом. 1 — 1.1, 1.2 (лист 61); пом. 4 — 1.1, 1.2 (лист 61).

1000 мм · печать 1:1

Изм.	Кол.уч	Лист	№ док.	Подп.	Дата
Разраб.		Кырлан А.С.			13.11.26
Пров.					
ГИП					
Н. контр.					
Утв.					

ГД-2026-003-АИ

Трёхкомнатная квартира

Общая площадь 78,95* м² · * размеры со скана, не замерены (реестр — л. 6–11, К-13)

Дизайн-проект интерьера трёхкомнатной квартиры

Стадия	Лист	Листов
РП	59	132

План потолков

М 1:75

Кырлан Александр Сергеевич

выпуск 13.11.2026 № 6f3a8abb2c · стр. 65 из 157


Разрезы и узлы потолков

Разрезы по потолкам с отметками уровней · узлы коробов и ниш · ведомость вырезов и закладных · размеры в мм

ПРЕДВАРИТЕЛЬНО · не для производства работ · открыто пунктов: 28 (реестр — л. 6–11)


Разрез 1–1 (М 1:40)

Пом. 6 Кухня-гостиная; линия разреза — план потолков, лист 59

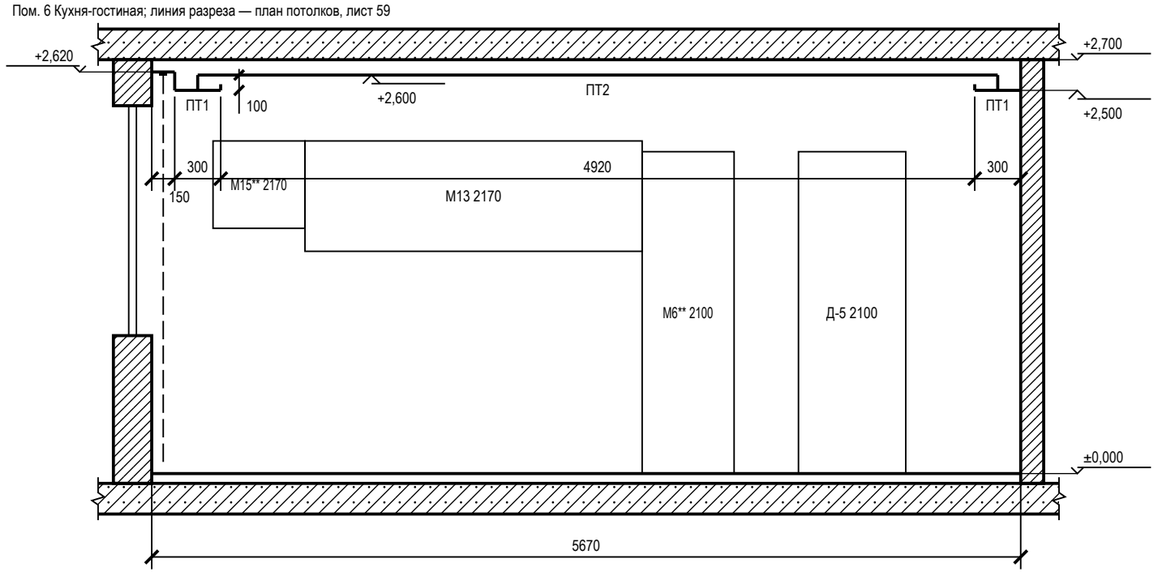

Разрез 2–2 (М 1:40)

Пом. 1 Спальня 1; линия разреза — план потолков, лист 59

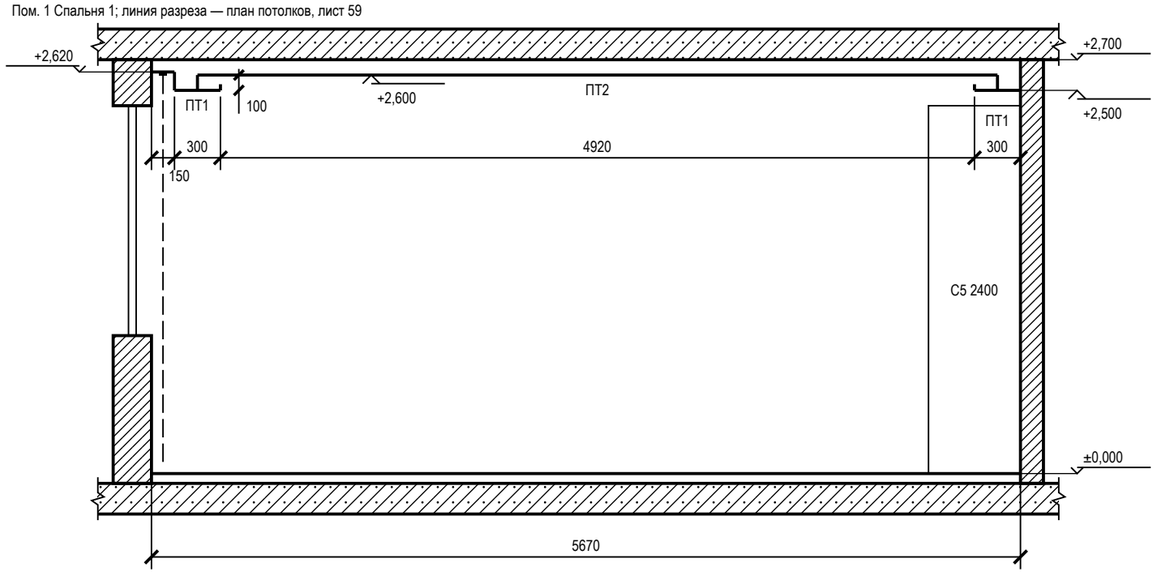

1 Короб с LED-подсветкой, теневой шов (М 1:10)

Пом. 1, 4, 6; карниз 150×100, щель под свет 60 мм

1 — плита перекрытия
2 — подвес прямой, шаг 1000 мм
3 — ПП 60×27: несущие через 500, основные через 1200 мм
4 — ГКЛ 12,5 по П113 — верхний уровень
5 — задняя стенка и бортик карниза — ГКЛ 12,5
6 — ПН 28×27 по периметру, к стене через 500 мм
7 — LED-лента в алюминиевом профиле
8 — теневой профиль: шов 15 мм, зазор 3 мм
9 — низ короба — ГКЛ 12,5 по ПП 60×27

2 Ниша под шторы (М 1:10)

Пом. 1, 4, 6; без подсветки; закладные под карниз — до обшивки

1 — закладная под карниз — брус 40×50
2 — карниз (шина), высота с верхом портьеры 100 мм
3 — стенка и потолок ниши — ГКЛ 12,5
4 — ПП 60×27 — каркас короба
5 — низ короба нижнего уровня — ГКЛ 12,5
6 — портьера
7 — стена с окном

Ведомость вырезов и закладных в потолке

Марка	Устройство	Кол.	Пом.
	Светильник встраиваемый (марки — план освещения)	39	1, 2, 4, 5, 6, 7, 8
	Светильник накладной (марки — план освещения)	1	3
	Светильник подвесной (марки — план освещения)	3	6
ИП1, ИП2, ИП4	Извещатель дымовой	3	1, 4, 6
ИП3, ИП5, ИП6	Извещатель тепловой	3	5, 6, 8
АР1**, АР2**	Точка доступа Wi-Fi, PoE	2	5, 6
ВР1…ВР3	Решётка вытяжная (вентилятор)	3	2, 6, 7
	Люк ревизии 300×300	3	1, 4, 6

Условные обозначения

- плита перекрытия в сечении
- стена в сечении
- потолок ГКЛ в сечении; под линией — марка потолка (план потолков)
- мебель и дверные проёмы за секущей плоскостью; число — марка и верх от чистого пола, мм
- портьера в нише под шторы

Допущения и предложения на листе

Основа листа: размеры сняты со скана плана заказчика по размерным цепочкам, контрольный обмер на объекте не выполнялся (К-13); высота потолка 2700 мм принята: на плане заказчика не указана (К-11); толщины стен приняты: наружные 250 мм, перегородки 150 мм (на плане 85–190 мм) (К-13); разрешённая мощность 15 кВт принята по типовой квартире, технических условий нет (К-14); утолщение стены 190 × 1360 мм и элемент 1470 × 160 мм плана заказчика не определены (К-12); ниши санузла 2 закрыты перегородкой и фальш-стеной: проектное решение, на плане заказчика ниша у входа открыта (К-18); несущие стены не определены: до технического заключения все существующие стены считаются несущими (К-20); окна существующие и сохраняются; подоконная доска и глубина откосов не заданы — приняты, не замерены (К-27); подрайон климата не задан — принят не северный (жилые от 2,5 м) (К-29).

Знак «**» — предложение проектировщика, заказчиком не утверждено (согласовать с заказчиком): ИЗ-5, К-8: М6, М15; ИЗ-17: АР1, АР2 — точка доступа Wi-Fi: число и места.

См. лист открытых вопросов (лист 6, запись К-8; лист 7, записи К-11–К-14, К-18, К-20; лист 8, записи К-27, К-29; лист 9, запись ИЗ-5; лист 11, запись ИЗ-17).

Примечания

1. Разрезы — по линиям 1–1, 2–2 на плане потолков (лист 59). Отметки — от ±0,000 чистого пола, м; размеры — мм.
2. Высоты мебели и дверных блоков за секущей плоскостью сверены с низом потолка над ними: верх ниже низа короба и поля.
3. ГКЛ 12,5 мм по каркасу П113; перепад уровней и бортик карниза — ГКЛ по ПП 60×27 (узел 1 — на этом листе). Ниша под шторы — на всю длину стены с окном, карниз на закладной до обшивки (узел 2 — на этом листе).
4. Толщины плит перекрытия и пирога пола показаны условно.
5. Сечения потолков по помещениям М 1:10 (отметки помещения, профили, подвесы, крепёж, изделия) — лист 61.
6. Ведомость вырезов и закладных в потолке — к плану потолков (лист 59): вырезы и закладные — до обшивки, марки светильников — по плану освещения.
7. Ведомость объёмов потолков (лист ГКЛ, профиль, подвесы, лента, блоки питания, люки) — на листе 61.

1000 мм · печать 1:1

Изм.	Кол.уч	Лист	№ док.	Подп.	Дата
Разраб.		Кырлан А.С.			13.11.26
Пров.					
ГИП					
Н. контр.					
Утв.					

ГД-2026-003-АИ

Трёхкомнатная квартира

Общая площадь 78,95* м² · * размеры со скана, не замерены (реестр — л. 6–11, К-13)

Дизайн-проект интерьера трёхкомнатной квартиры

Стадия	Лист	Листов
РП	60	132

Разрезы и узлы потолков

М 1:40; 1:10

Кырлан Александр Сергеевич


выпуск 13.11.2026 № 6f3a8abb2c · стр. 66 из 157

Сечения потолков М 1:10

Пом. 1, 4, 6 · профили, подвесы, крепёж, изделия · размеры в мм

Сечение 1.1. Короб с LED-подсветкой, теневой шов (М 1:10)


Пом. 1 Спальня 1, 4 Спальня 2, 6 Кухня-гостиная; карниз 150×100, щель под свет 60 мм

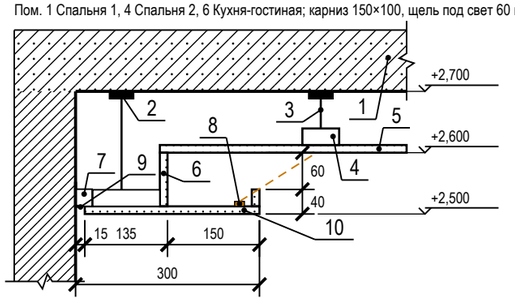

1 — плита перекрытия
2 — анкер-клин к плите — по одному на подвес
3 — подвес прямой, шаг 1000 мм
4 — ПП 60×27: несущие через 500, основные через 1200 мм; соединители одноуровневые, шурупы LN 3,5×9
5 — ГКЛ 12,5 по П113 — верхний уровень; шурупы TN 3,5×25 через 170 мм
6 — задняя стенка и бортик карниза — ГКЛ 12,5
7 — ПН 28×27 по периметру — дюбель-гвоздь через ≤ 500 мм, не менее 3 на профиль
8 — LED-лента 9,6 Вт/м, 24 В в алюминиевом профиле
9 — теневой профиль: шов 15 мм, зазор 3 мм
10 — низ короба — ГКЛ 12,5 по ПП 60×27

Сечение 1.2. Ниша под шторы (М 1:10)

Пом. 1 Спальня 1, 4 Спальня 2, 6 Кухня-гостиная; без подсветки; закладные под карниз — до обшивки

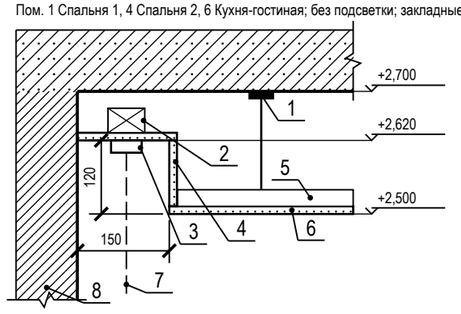

1 — анкер-клин к плите — по одному на подвес; подвес прямой, шаг 1000 мм
2 — закладная под карниз — брус 40×50
3 — карниз (шина), высота с верхом портьеры 100 мм
4 — стенка и потолок ниши — ГКЛ 12,5
5 — ПП 60×27 — каркас короба, основные через 1200 мм; соединители одноуровневые, шурупы LN 3,5×9
6 — низ короба нижнего уровня — ГКЛ 12,5; шурупы TN 3,5×25 через 170 мм
7 — портьера
8 — стена с окном

Ведомость объёмов потолков

Позиция	Ед.	Кол.	Пом.
Лист ГКЛ 12,5	м²	86,10	1, 4, 5, 6, 8
Лист ГКЛВ 12,5	м²	6,72	2, 7
Борта и карнизы (входят в площади листов выше)	м²	15,71	1, 4, 6
Профиль ПП 60×27	м	234,46	1, 2, 4, 5, 6, 7, 8
Профиль ПН 28×27	м	261,30	1, 2, 4, 5, 6, 7, 8
Подвес прямой	шт.	114	1, 2, 4, 5, 6, 7, 8
Анкер-клин к плите	шт.	114	1, 2, 4, 5, 6, 7, 8
Шуруп TN 3,5×25	шт.	2135	1, 2, 4, 5, 6, 7, 8
Лента армирующая для швов	м	111,38	1, 2, 4, 5, 6, 7, 8

Ведомость объёмов потолков (окончание)

Позиция	Ед.	Кол.	Пом.
Шпаклёвка для швов	кг	37,13	1, 2, 4, 5, 6, 7, 8
Грунтовка (швы)	л	9,28	1, 2, 4, 5, 6, 7, 8
Лента разделительная по периметру	м	91,46	1, 2, 4, 5, 6, 7, 8
Сплошная шпаклёвка и окраска (площадь развёртки)	м²	92,82	1, 2, 4, 5, 6, 7, 8
Лента LED	м	49,90	1, 4, 6
Требуемая мощность блоков питания	Вт	623	1, 4, 6
Установленная мощность блоков питания	Вт	700	1, 4, 6
Блок питания LED	шт.	3	1, 4, 6
Люк ревизии	шт.	3	1, 4, 6

Условные обозначения

— · — LED-лента в нише подсветки (карниз короба, ниша фигуры)

Допущения и предложения на листе

Основа листа: размеры сняты со скана плана заказчика по размерным цепочкам, контрольный обмер на объекте не выполнялся (К-13); высота потолка 2700 мм принята: на плане заказчика не указана (К-11); толщины стен приняты: наружные 250 мм, перегородки 150 мм (на плане 85–190 мм) (К-13); разрешённая мощность 15 кВт принята по типовой квартире, технических условий нет (К-14); утолщение стены 190 × 1360 мм и элемент 1470 × 160 мм плана заказчика не определены (К-12); ниши санузла 2 закрыты перегородкой и фальш-стеной: проектное решение, на плане заказчика ниша у входа открыта (К-18); несущие стены не определены: до технического заключения все существующие стены считаются несущими (К-20); окна существующие и сохраняются; подоконная доска и глубина откосов не заданы — приняты, не замерены (К-27); подрайон климата не задан — принят не северный (жилые от 2,5 м) (К-29).
См. лист открытых вопросов (лист 7, записи К-11–К-14, К-18, К-20; лист 8, записи К-27, К-29).

Примечания

1. Сечения потолков М 1:10 по помещениям с нишами LED и нишами под шторы: отметки и размеры этого помещения от ±0,000 чистого пола (м, мм). Положение — по плану потолков (лист 59): короб и ниша LED — по линиям ленты, ниша под шторы — у стены с окном; типовые узлы по группам помещений — на листе 60.
2. Крепёж: подвес прямой к плите на анкер-клине — по одному на подвес (Knauf П113); ПН к стенам — дюбель-гвоздь через ≤ 500 мм, не менее 3 на профиль (серия 1.045.9-2.08); лист 12,5 — шурупы TN 3,5×25 через 170 мм (СП 163, табл. 15); профили между собой — соединители одноуровневые, шурупы LN 3,5×9.
3. Изделие карниза, профиля LED и галтели подписано артикулом из данных; где артикул не выбран, сечение дано по габаритам из данных (ширина и глубина ниши, щель под свет), изделие подбирается по ним.
4. Ведомость объёмов — по геометрии плана потолков: Лист ГКЛ 12,5 — плоскости уровней + борта (без арочных участков); Лист ГКЛВ 12,5 — плоскости уровней + борта; Борта и карнизы — длина перепада × перепад; Профиль ПП 60×27 — S × (1/шаг несущ. + 1/шаг осн.) + стойки бортов; Профиль ПН 28×27 — периметр стен + 2 × перепады + карнизы; Подвес прямой — по раскладке: S уровня / (шаг осн. × шаг подвесов), пояс уже шага — ряд вдоль пояса, фигура — по контуру; шаг подвесов — не больше табл. 14 СП 163; Анкер-клин к плите — по одному на подвес (Knauf П113); Шуруп TN 3,5×25 — 23 шт./м² (Knauf П113, табл. 2 альбома П 11); Лента армирующая для швов — 1,2 м/м² листа (Knauf); Шпаклёвка для швов — 0,4 кг/м² листа, только швы (Knauf); Грунтовка (швы) — 0,1 л/м² листа, только швы (Knauf); Лента разделительная по периметру — периметр стен под потолком ГКЛ; Сплошная шпаклёвка и окраска (площадь развёртки) — плоскости + борта; расход — по паспорту материала (норма расхода на сплошной слой не подтверждена); Лента LED — по оси карниза и ниши фигуры (план потолков); Требуемая мощность блоков питания — Вт/м × длина × 1,3; Установленная мощность блоков питания — сумма мощностей блоков по плану освещения; Блок питания LED — блоки потолочных лент по плану освещения (БП1, БП2, БП4); Люк ревизии — план потолков; без запаса на подрезку (при закупке листа: ×1,075 при S > 20 м², ×1,175 — 10–20 м², ×1,275 — < 10 м²).

1000 мм · печать 1:1

Изм.	Кол.уч	Лист	№ док.	Подп.	Дата
Разраб.		Кырлан А.С.			13.11.26
Пров.					
ГИП					
Н. контр.					
Утв.					

ГД-2026-003-АИ

Трёхкомнатная квартира

Общая площадь 78,95* м² · * размеры со скана, не замерены (реестр — л. 6–11, К-13)

Дизайн-проект интерьера трёхкомнатной квартиры

Стадия	Лист	Листов
РП	61	132

Сечения потолков М 1:10

М 1:10


Кырлан Александр Сергеевич

выпуск 13.11.2026 № 6f3a8abb2c · стр. 67 из 157


Раскладка плитки. Планы полов

Раскладка от чистовых размеров · размеры в мм · отметки от ±0,000

Фрагмент 1. Ванная (пом. 2). Пол 600×600, шов 2 мм (М 1:20)

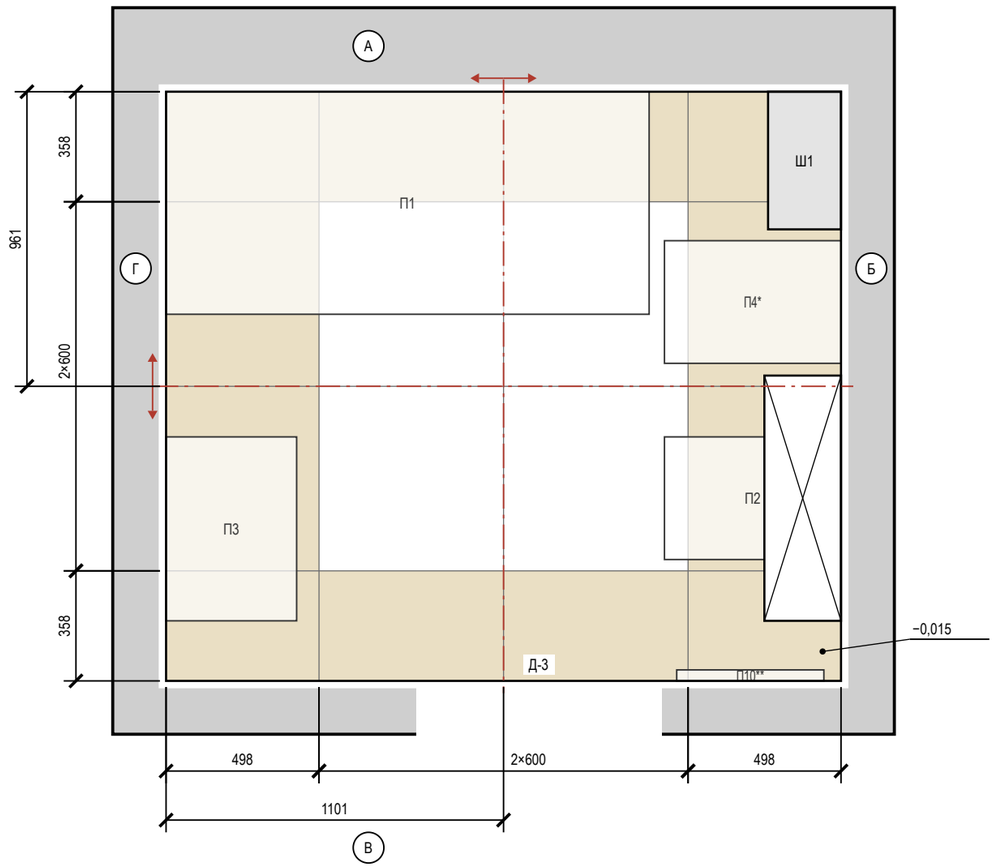

Фрагмент 2. Санузел 2 (пом. 7). Пол 600×600, шов 2 мм (М 1:20)

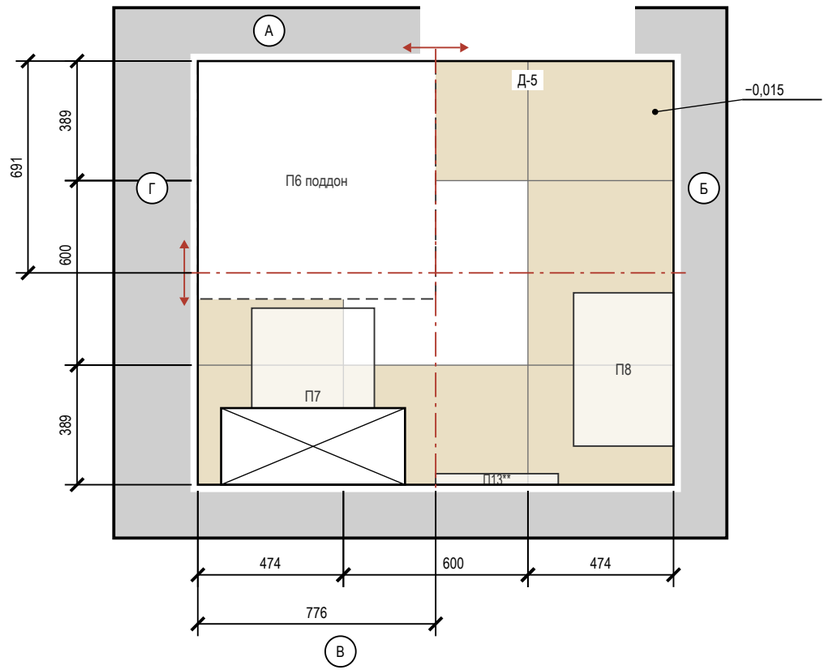

Примечания

1. Раскладка от чистовых размеров: стены санузлов теряют 10 + 5 + 9 = 24 мм на сторону (штукатурка, клей, плитка); подрезки — чистые, без шва.
2. Старт — от центра помещения (штрихпунктир, стрелки направление укладки); размер старта — от чистовых стен Г и А.
3. Раскладка пола «Прихожая» и фартука «Кухня-гостиная» на листе «Раскладка плитки. Прихожая. Фартук кухни».
4. Калибр партии не задан — до укладки замерить (рабочий размер W, ГОСТ 13996-2019) и пересчитать подрезки.
5. Количество: целые по раскладке + по одной на подрезку, запас 10 %; один артикул — одна партия и тон. Исключены поддон, короб, проёмы и места за коробом; S — по чистым граням: стены нетто = зона облицовки по ведомости отделки − место за коробом инсталляции 3,33 м² (плитку за коробом не кладут), короб — отдельной строкой.
6. Клей C2 TE S1 Ceresit CM 17; C2 TE S1 (ГОСТ Р 56387-2018), затирка CG2WA Mapei Ultracolor Plus 132; CG2WA; расход — по ТУ выбранной марки.
7. Гидроизоляция: пол и стены 200 мм от ЧП; над ванной до 2000 и 300 мм за борт (пом. 2), у душа — до 2000 и 500 мм за поддон (пом. 7) (см. развёртки); акт скрытых работ, пролив 24 ч.
8. Швы пола совмещены со швами стены А; по периметру демпферная лента.
9. Отметка чистого пола −0,015, порог 15 мм; стык с соседним покрытием — по оси полотна двери.

Ведомость материалов

Материал	Класс, код	Норма расхода	Кол-во
Затирка	CG2WA Mapei Ultracolor Plus 132	(a+b)/ab·шов·t·1,6	3,1 кг
Затирка	CG2WA	(a+b)/ab·шов·t·1,6	0,7 кг
Клей	C2 TE S1 Ceresit CM 17	1,2 кг/м²·мм, слой 5	249 кг (10 меш.)
Клей	C2 TE S1	1,2 кг/м²·мм, слой 5	59 кг (3 меш.)
Гидроизоляция	обмазочная, 2 слоя: пол, стены по периметру и зоны замачивания	по ТУ	20,0 м²
Демпф. лента	по периметру пола из плитки		22,4 м

Условные обозначения

- плитка целая; тонкая линия — шов
- плитка с подрезкой (размер — на цепочке)
- ось старта; стрелки — направление укладки
- сантехприбор: габарит, высота по практике
- поддон душа — плитку пола под ним не кладут
- короб инсталляции: плитка пола — до короба
- короб стояков (Ш…): плитка пола — до короба
- отметка чистого пола на полке выноски, м
- (А) обозначение стены А–Г (как на развёртках)

Ведомость плитки

Помещение, поверхность	Плитка, код	Формат	Шов	S, м²	Целых	Подр.	С запасом
Ванная, пол	аналог: керамогранит под травертин	600×600	2	4,43	4	12	18
Ванная, стены А–Г	аналог: керамогранит под травертин	600×1200	2	16,00	9	20	33
Ванная, короб стояков Ш1 248×459	аналог: керамогранит под травертин	600×1200	2	1,65	0	4	6
Ванная, короб инсталляции	аналог: керамогранит под травертин	600×1200	2	1,76	0	6	7
Санузел 2, пол	аналог: керамогранит под травертин	600×600	2	2,29	0	8	9
Санузел 2, стены А–Г	аналог: керамогранит под травертин	600×1200	2	12,38	5	19	28
Санузел 2, короб инсталляции	аналог: керамогранит под травертин	600×1200	2	1,47	1	3	5
Прихожая, пол	аналог: керамогранит ректифицированный под травертин, матовый	600×1200	2	7,13	2	10	14
Кухня-гостиная, фартук (ст. В)	аналог: керамогранит под травертин, матовый	1200×600	2	1,85	0	4	5
Итого 600×600				6,72	4	20	27
Итого 600×1200				**42,24**	**17**	**66**	**98**

Допущения и предложения на листе. Знак «*» принято (замерить). Знак «**» предложено (согласовать): пол пом. 2, 7, стены пом. 2, 7. См. лист открытых вопросов (листы 6–11).

1000 мм · печать 1:1

Изм.	Кол.уч	Лист	№ док.	Подп.	Дата
Разраб.		Кырлан А.С.			13.11.26
Пров.					
ГИП					
Н. контр.					
Утв.					

ГД-2026-003-АИ

Трёхкомнатная квартира

Общая площадь 78,95* м² · * размеры со скана, не замерены (реестр — л. 6–11, К-13)

Дизайн-проект интерьера трёхкомнатной квартиры

Стадия	Лист	Листов
РП	62	132

Раскладка плитки. Планы полов

М 1:20


Кырлан Александр Сергеевич

выпуск 13.11.2026 № 6f3a8abb2c · стр. 68 из 157


Раскладка плитки. Прихожая. Фартук кухни

Раскладка от чистовых размеров · размеры в мм · высоты фартука от чистого пола

Фрагмент 1. Прихожая (пом. 5). Пол 600×1200, шов 2 мм (М 1:20)

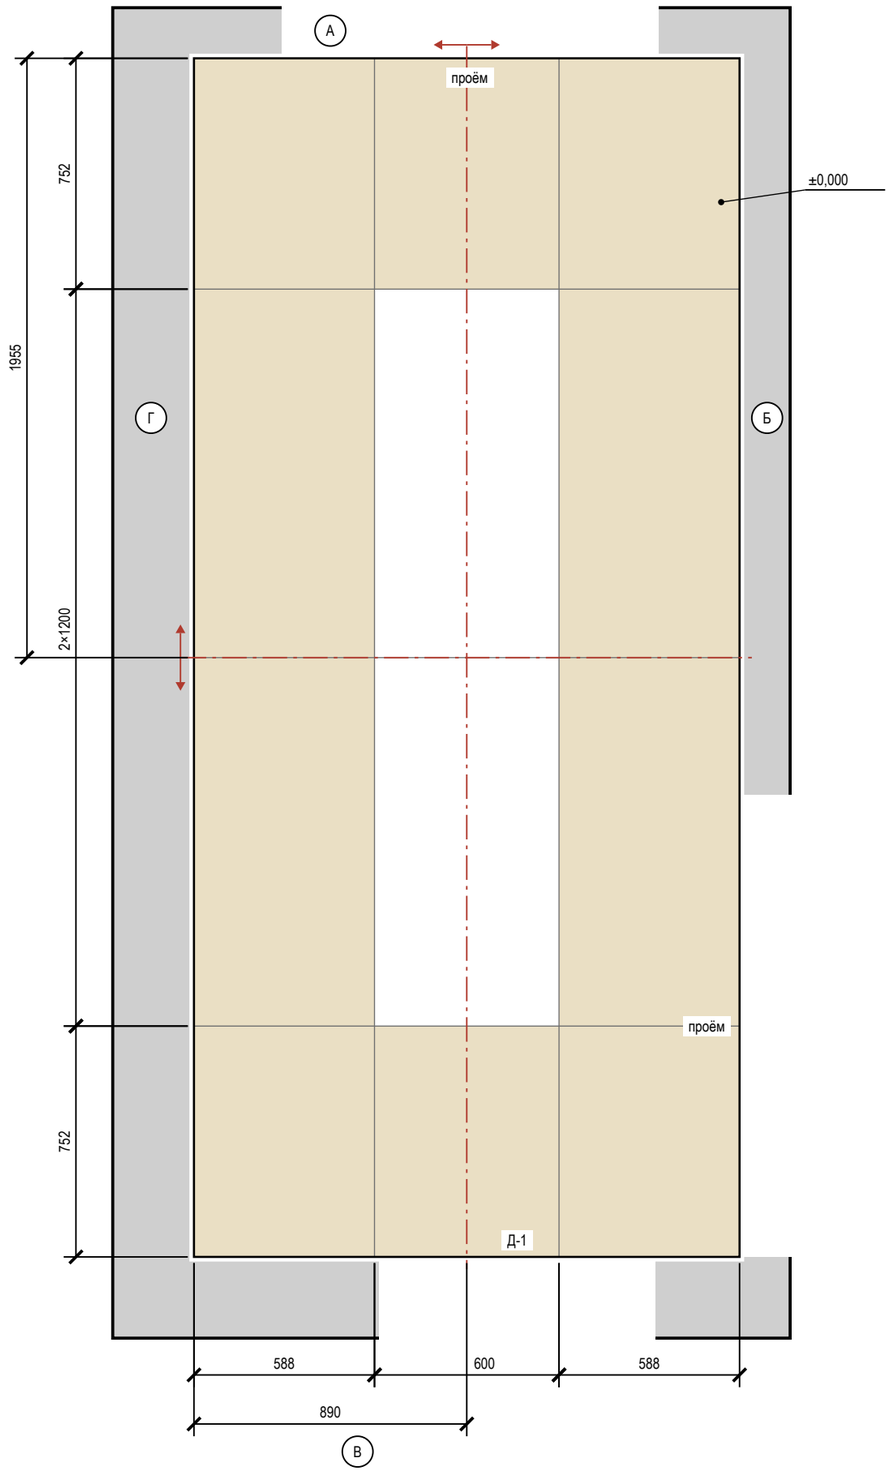

Фрагмент 2. Кухня-гостиная (пом. 6), фартук, стена В. 1200×600, шов 2 мм (М 1:20)

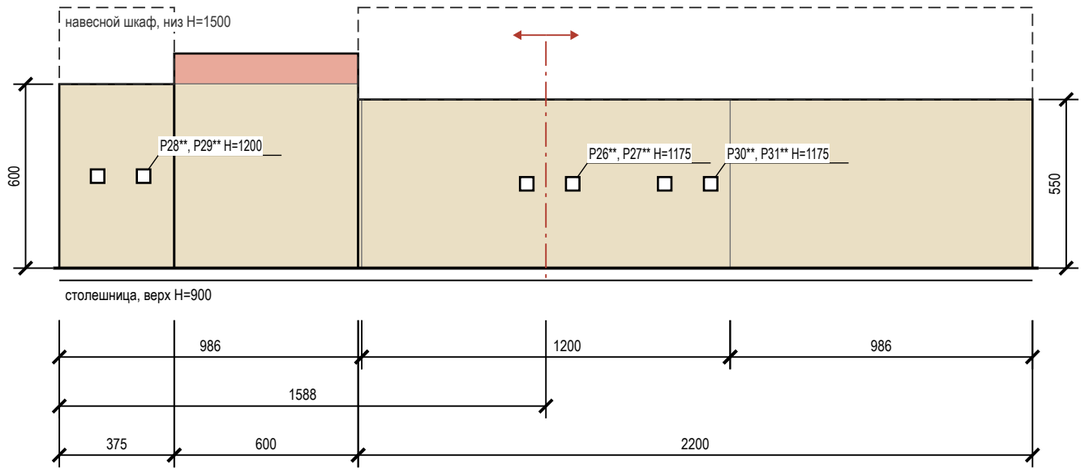

Условные обозначения

- плитка целая; тонкая линия — шов
- плитка с подрезкой (размер — на цепочке)
- ось старта; стрелки — направление укладки
- электроточка: марка и H — по листам ЭОМ
- столешница (верх)
- навесной шкаф над фартуком
- отметка чистого пола на полке выноски, м
- (А) обозначение стены А–Г (как на развёртках)

Подсчёт плитки

Поверхность	Формат	S, м²	Целых	Подр.	С запасом
Прихожая, пол	600×1200	7,13	2	10	14
Кухня-гостиная, фартук (ст. В)	1200×600	1,85	0	4	5

Допущения и предложения на листе. Основа листа: размеры сняты со скана плана заказчика по размерным цепочкам, контрольный обмер на объекте не выполнялся (К-13); высота потолка 2700 мм принята: на плане заказчика не указана (К-11); толщины стен приняты: наружные 250 мм, перегородки 150 мм (на плане 85–190 мм) (К-13); разрешённая мощность 15 кВт принята по типовой квартире, технических условий нет (К-14); утолщение стены 190 × 1360 мм и элемент 1470 × 160 мм плана заказчика не определены (К-12); ниши санузла 2 закрыты перегородкой и фальш-стеной: проектное решение, на плане заказчика ниша у входа открыта (К-18); несущие стены не определены: до технического заключения все существующие стены считаются несущими (К-20); окна существующие и сохраняются; подоконная доска и глубина откосов не заданы — приняты, не замерены (К-27); подрайон климата не задан — принят не северный (жилые от 2,5 м) (К-29). Знак «**» — предложение проектировщика, заказчиком не утверждено (согласовать с заказчиком): P26, P27, P30, P31 — Сдвиг под раскладку плитки фартука (стена В) на 75 мм выше — ось на шве или в центре плитки, привязка по таблице листа; P28, P29 — Сдвиг под раскладку плитки фартука (стена В) на 100 мм выше — ось на шве или в центре плитки, привязка по таблице листа; К-23: пол пом. 5, 6, плинтус пом. 5, 6, фартук пом. 6 — артикул изделия не выбран: позиция описана характеристиками («аналог по характеристикам»), артикул выбирается при закупке. См. лист открытых вопросов (лист 7, записи К-11–К-14, К-18, К-20; лист 8, записи К-23, К-27, К-29); по листу — К-23.

Примечания

1. Прихожая: керамогранит 600×1200, длинная сторона — вдоль стен Б и Г, шов 2 мм, прямая раскладка от центра. Стены окрашены: раскладка от чистового контура минус штукатурка и шпаклёвка 15 мм на сторону (принято); подрезки 588 / 752 мм, срез — под плинтус.
2. Прихожая: деформационный зазор по периметру 8–10 мм под плинтусом; в проёмах — стык с соседним покрытием по оси полотна двери. Клей C2 TE S1, затирка CG2WA.
3. Фартук, Кухня-гостиная: 1200×600 горизонтально, шов 2 мм; зоны 2200 мм — 900…1450, 600 мм — 900…1600, 375 мм — 900…1500 (от столешницы до низа навесного шкафа, без шкафа — 700 мм). Старт от центра участка, подрезки 986 мм. Площадь 1,85 м² — как в ведомости отделки.
4. Фартук — после монтажа столешницы, низ на 2–3 мм выше неё, шов со столешницей — санитарный герметик; навесные шкафы — после фартука. Торцы у пенала и стены — профиль или запил 45°.
5. Фартук, Кухня-гостиная: в зоне до отм. 1600 верхний ряд подрезан 98 мм — меньше 1/3 плитки; полоса прикрыта корпусом навесного модуля и на виду не остаётся. Раскладкой не снимается: убрать подрезку можно, только выровняв низ этого модуля с соседними (1450 мм) — решение мебельщика.
6. Клей, затирка и итог по форматам — в ведомостях листа «Раскладка плитки. Планы полов».

1000 мм · печать 1:1

Изм.	Кол.уч	Лист	№ док.	Подп.	Дата
Разраб.		Кырлан А.С.			13.11.26
Пров.					
ГИП					
Н. контр.					
Утв.					

ГД-2026-003-АИ

Трёхкомнатная квартира

Общая площадь 78,95* м² · * размеры со скана, не замерены (реестр — л. 6–11, К-13)

Дизайн-проект интерьера трёхкомнатной квартиры

Стадия	Лист	Листов
РП	63	132

Раскладка плитки. Прихожая. Фартук кухни

М 1:20


Кырлан Александр Сергеевич

выпуск 13.11.2026 № 6f3a8abb2c · стр. 69 из 157

Раскладка плитки. Ванная. Развёртки стен

ПРЕДВАРИТЕЛЬНО · не для производства работ · открыто пунктов: 28 (реестр — л. 6–11)

Пом. 2 · вид изнутри помещения · размеры в мм · высоты от чистого пола, отметки от ±0,000

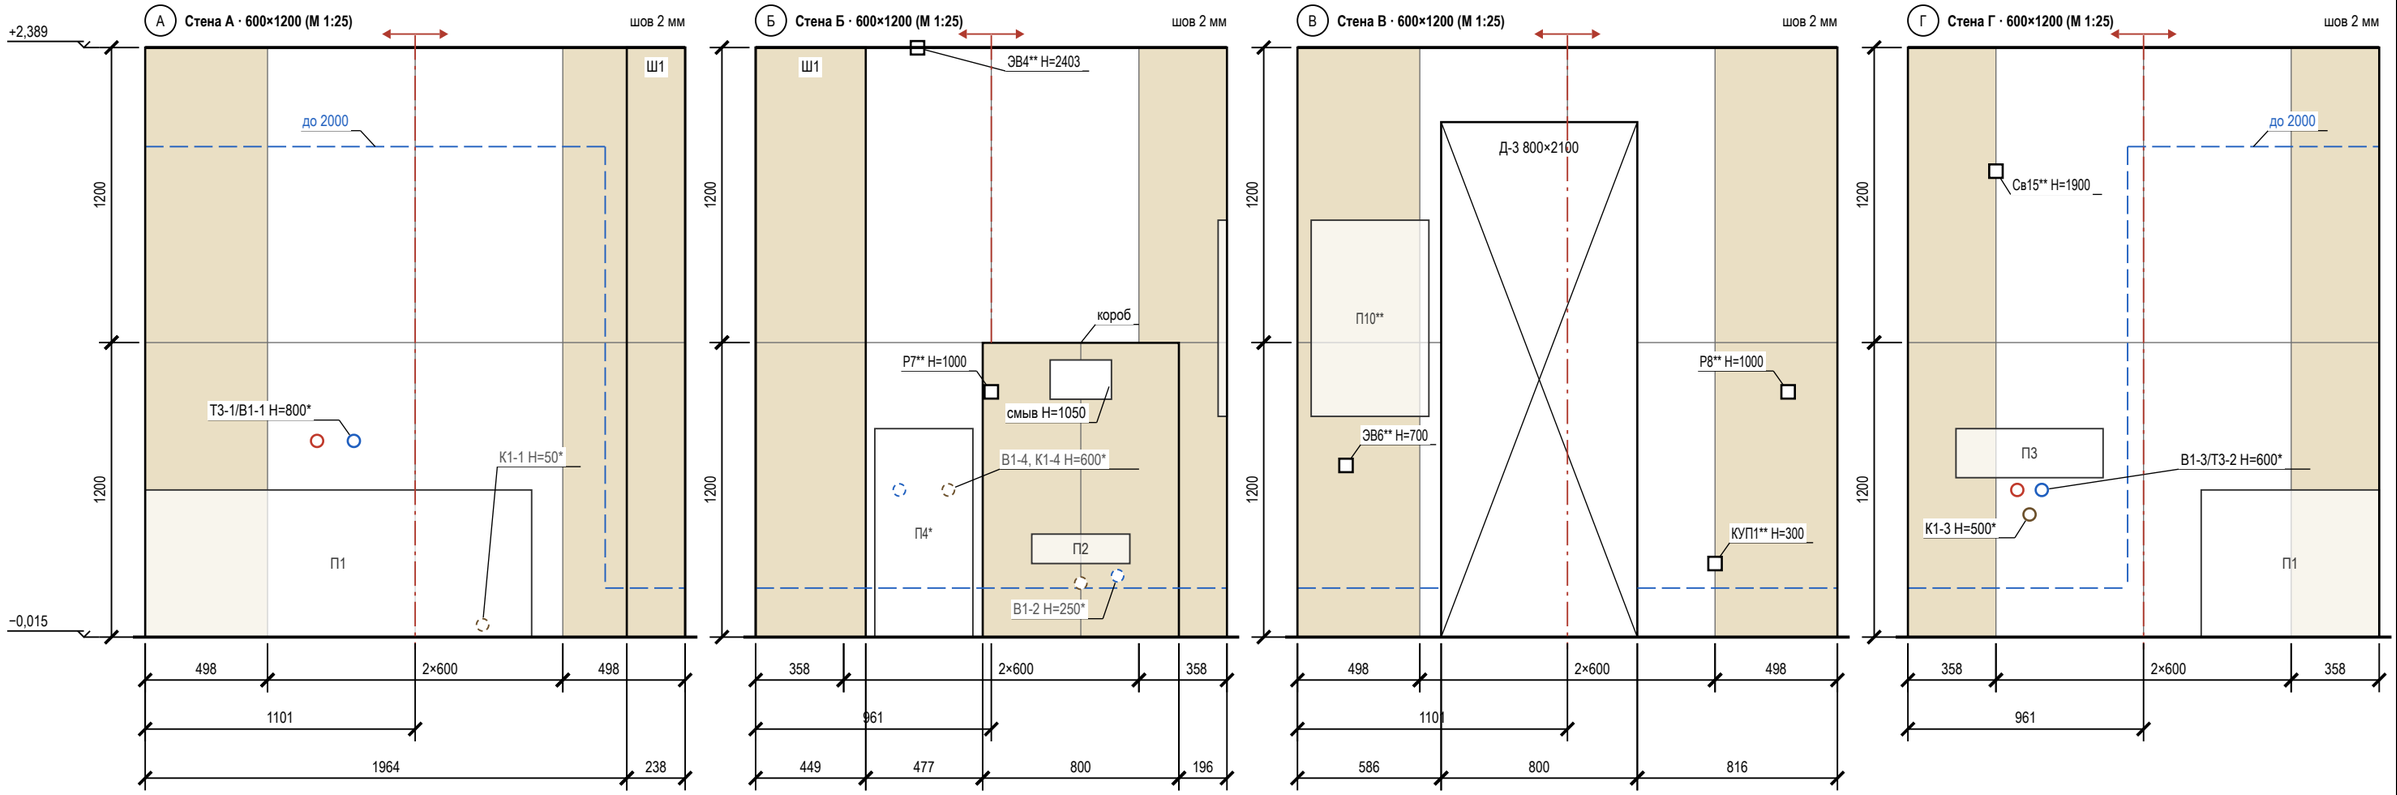

Подсчёт плитки по стенам и коробу

Поверхность	L × H, мм	S, м²	Целых	Подр.	С запасом	Подрезки: край / верх, мм
стена А	2202 × 2404	4,84	4	4	9	498 / 498; целый ряд
Ш1 248×459, ст. А	238 × 2404	0,57	0	2	3	лицо 238
стена Б	1922 × 2404	2,70	1	4	6	358 / 358; целый ряд
Ш1 248×459, ст. Б	449 × 2404	1,08	0	2	3	лицо 449
короб (ст. Б)	800×1200×250	1,76	0	6	7	лицо 399 / 399; бок. 250
стена В	2202 × 2404	3,73	0	8	9	498 / 498; целый ряд
стена Г	1922 × 2404	4,74	4	4	9	358 / 358; целый ряд
Итого		**19,41**	**9**	**30**	**46**	

Условные обозначения

- плитка целая; тонкая линия — шов
- плитка с подрезкой (размер — на цепочке)
- ось старта; стрелки — направление укладки
- верх гидроизоляции: 200 от ЧП, в мокрой зоне — «до …»
- проём — не облицовывается
- сантехприбор: габарит, высота по практике
- короб инсталляции, в нём кнопка смыва 250×160
- грань короба стояков (Ш…): своя сетка, за коробом плитку не кладут
- вывод В1 (код — в ведомости привязок)
- вывод Т3 (код — в ведомости привязок)
- вывод К1 (код — в ведомости привязок)
- вывод за прибором / в коробе (не на сетке)
- электроточка: марка и Н — по листам ЭОМ
- отметка уровня, м: ±0,000 — чистый пол жилых помещений
- низ потолка; серая полоса — стена без плитки
- (А) обозначение стены А–Г (как на развёртках)

Примечания

1. Вид изнутри, стены по часовой стрелке А → Г. Высоты — от чистого пола (−0,015), отметки — от ±0,000. Раскладка от чистовых размеров (штукатурка 10 + клей 5 + плитка 9 мм), подрезки чистые; старт — от оси стены, ряды от пола целыми.
2. Облицовка до потолка (+2,389).
3. Открытые выводы и электроточки — на шве или в центре плитки (допуск 10 мм; плитка от 900 мм по высоте — на шве или не ближе 60 мм к нему).
4. Выводы ВК стоят по оси прибора и с прибором не двигаются — привязки по «Плану выводов сантехники» без сдвига; вне сетки (Т3-1/В1-1, В1-3/Т3-2, К1-3) отверстие в плитке коронкой по той же привязке, плитку не сдвигать.
5. Выводы — по «Плану выводов сантехники», электроточки — по ЭОМ, «*» — высота по практике; за приборами и в коробе (К1-1, В1-2, К1-2, В1-4, К1-4) штриховым кольцом.
6. Гидроизоляция: 200 мм от ЧП по периметру; над ванной — до 2000 и 300 мм за борт (СП 29.13330.2011, п. 7.2 — на высоту замачивания); углы — лентой; акт скрытых работ, пролив.
7. Короб 800×1200×250: лицо 399 / 399 мм от оси кнопки смыва, боковины, полка; углы — запил 45° или профиль; за коробом плитку не кладут.
8. Между коробом и углом полоса 196 мм — довести короб до угла.
9. Короб стояков Ш1: грани 238 мм (ст. А), 449 мм (ст. Б) — плиткой стен по рядам стены, целая плитка от наружного угла; угол — запил 45° или профиль; за коробом плитку не кладут. Люк 300×400 — на грани ст. Б: высота — по месту ревизии стояка (положение стояков сверяется на объекте), кромки дверцы по швам сетки, дверца нажимная под плитку.

1000 мм · печать 1:1

Допущения и предложения на листе. Знак «*» принято (замерить): отметка существующего пола. Знак «**» предложено (согласовать): пол пом. 2, стены пом. 2. См. лист открытых вопросов (листы 6–11).

Изм.	Кол.уч	Лист	№ док.	Подп.	Дата
Разраб.		Кырлан А.С.			13.11.26
Пров.					
ГИП					
Н. контр.					
Утв.					

ГД-2026-003-АИ

Трёхкомнатная квартира

Общая площадь 78,95* м² · * размеры со скана, не замерены (реестр — л. 6–11, К-13)

Дизайн-проект интерьера трёхкомнатной квартиры

Стадия	Лист	Листов
РП	64	132

Раскладка плитки. Ванная. Развёртки стен

М 1:25


Кырлан Александр Сергеевич

выпуск 13.11.2026 № 6f3a8abb2c · стр. 70 из 157

Раскладка плитки. Санузел 2. Развёртки стен

ПРЕДВАРИТЕЛЬНО · не для производства работ · открыто пунктов: 28 (реестр — л. 6–11)

Пом. 7 · вид изнутри помещения · размеры в мм · высоты от чистого пола, отметки от ±0,000

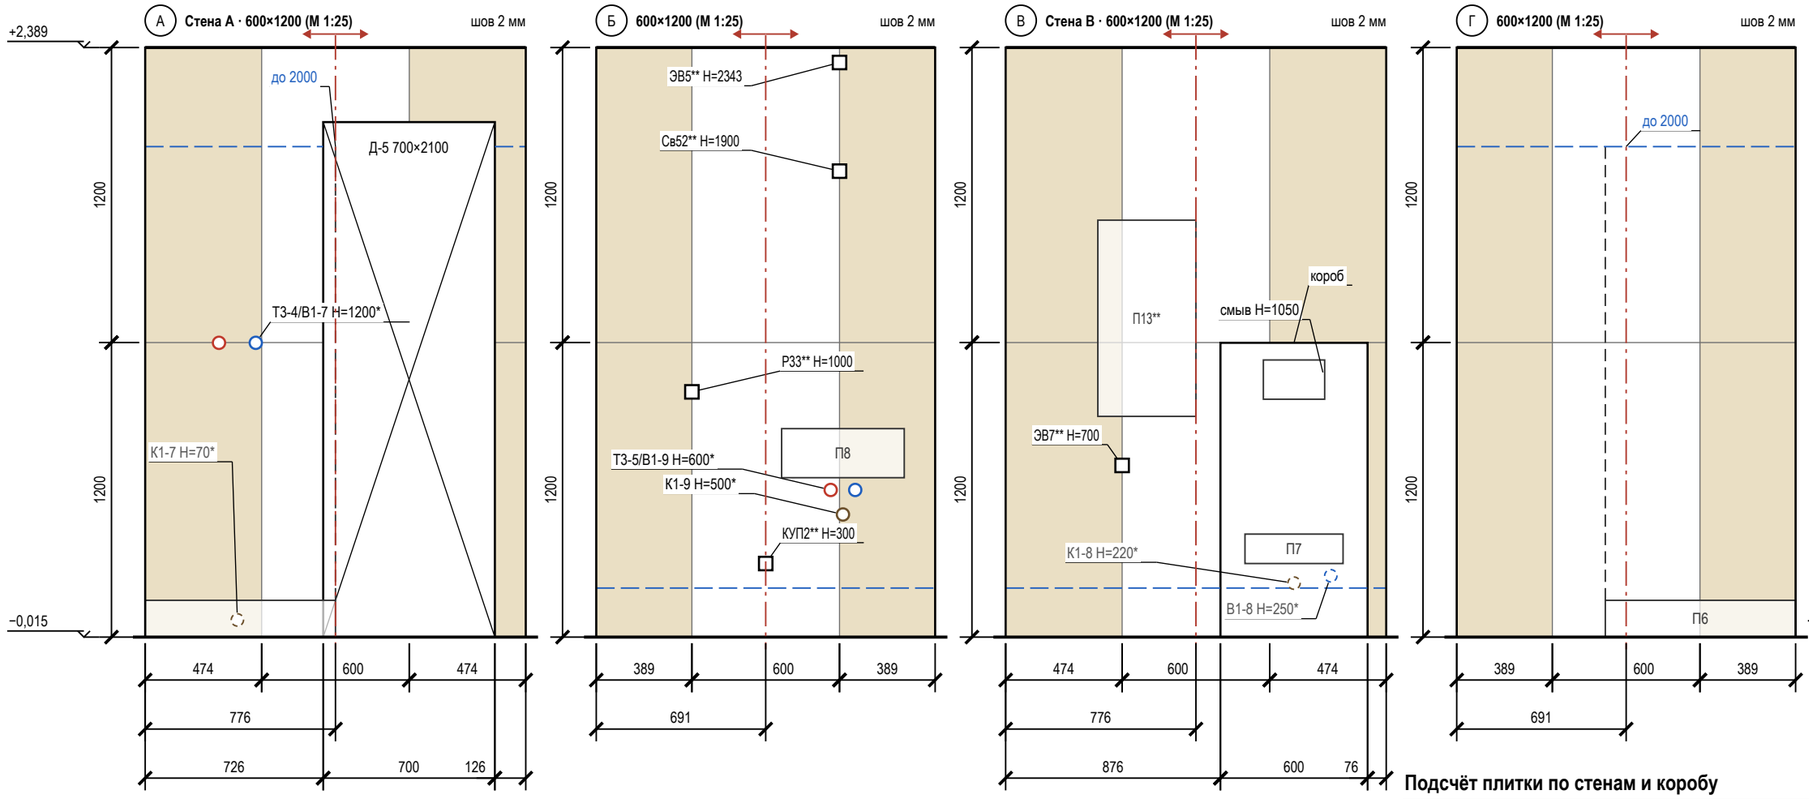

Условные обозначения

- плитка целая; тонкая линия — шов
- плитка с подрезкой (размер — на цепочке)
- ось старта; стрелки — направление укладки
- верх гидроизоляции: 200 от ЧП, в мокрой зоне — «до …»
- проём — не облицовывается
- сантехприбор: габарит, высота по практике
- граница душевой зоны (ограждение)
- короб инсталляции, в нём кнопка смыва 250×160
- вывод В1 (код — в ведомости привязок)
- вывод Т3 (код — в ведомости привязок)
- вывод К1 (код — в ведомости привязок)
- вывод за прибором / в коробе (не на сетке)
- электроточка: марка и Н — по листам ЭОМ
- отметка уровня, м: ±0,000 — чистый пол жилых помещений
- низ потолка; серая полоса — стена без плитки
- (А) обозначение стены А–Г (как на развёртках)

Подсчёт плитки по стенам и коробу

Поверхность	L × H, мм	S, м²	Целых	Подр.	С запасом	Подрезки: край / верх, мм
стена А	1552 × 2404	2,38	0	6	7	474 / 474; целый ряд
стена Б	1382 × 2404	3,44	2	4	7	389 / 389; целый ряд
стена В	1552 × 2404	3,13	1	5	7	474 / 474; целый ряд
короб (ст. В)	600×1200×250	1,47	1	3	5	лицо 600; бок. 250
стена Г	1382 × 2404	3,44	2	4	7	389 / 389; целый ряд
Итого		**13,85**	**6**	**22**	**33**	

Примечания

1. Вид изнутри, стены по часовой стрелке А → Г. Высоты — от чистого пола (−0,015), отметки — от ±0,000. Раскладка от чистовых размеров (штукатурка 10 + клей 5 + плитка 9 мм), подрезки чистые; старт — от оси стены, ряды от пола целыми.
2. Облицовка до потолка (+2,389).
3. Открытые выводы и электроточки — на шве или в центре плитки (допуск 10 мм; плитка от 900 мм по высоте — на шве или не ближе 60 мм к нему).
4. Выводы ВК стоят по оси прибора и с прибором не двигаются — привязки по «Плану выводов сантехники» без сдвига; вне сетки (Т3-4/В1-7, Т3-5/В1-9, К1-9) отверстие в плитке коронкой по той же привязке, плитку не сдвигать.
5. Выводы — по «Плану выводов сантехники», электроточки — по ЭОМ, «*» — высота по практике; за приборами и в коробе (К1-7, В1-8, К1-8) — штриховым кольцом.
6. Гидроизоляция: 200 мм от ЧП по периметру; у душа — до 2000 и 500 мм за поддон (СП 29.13330.2011, п. 7.2 — на высоту замачивания); углы — лентой; акт скрытых работ, пролив.
7. Короб 600×1200×250: лицо 600 мм от оси кнопки смыва, боковины, полка; углы — запил 45° или профиль; за коробом плитку не кладут.
8. Между коробом и углом полоса 76 мм — довести короб до угла.

Допущения и предложения на листе. Основа листа: размеры сняты со скана плана заказчика по размерным цепочкам, контрольный обмер на объекте не выполнялся (К-13); высота потолка 2700 мм принята: на плане заказчика не указана (К-11); толщины стен приняты: наружные 250 мм, перегородки 150 мм (на плане 85–190 мм) (К-13); разрешённая мощность 15 кВт принята по типовой квартире, технических условий нет (К-14); утолщение стены 190 × 1360 мм и элемент 1470 × 160 мм плана заказчика не определены (К-12); ниши санузла 2 закрыты перегородкой и фальш-стеной: проектное решение, на плане заказчика ниша у входа открыта (К-18); несущие стены не определены: до технического заключения все существующие стены считаются несущими (К-20); окна существующие и сохраняются; подоконная доска и глубина откосов не заданы — приняты, не замерены (К-27); подрайон климата не задан — принят не северный (жилые от 2,5 м) (К-29). Знак «*» — принято, не замерено (замерить): К-13: отметка существующего пола. Знак «**» — предложено, не утверждено (согласовать): Св52; ИЗ-1: ЭВ7; ИЗ-2, К-2, К-23: пол пом. 7; ИЗ-8: ЭВ5, КУП2; К-2, К-23: стены пом. 7. См. лист открытых вопросов (лист 6, записи К-2, К-7; лист 7, записи К-11–К-14, К-18, К-20; лист 8, записи К-23, К-27, К-29; лист 9, записи ИЗ-1, ИЗ-2, ИЗ-4, ИЗ-8, ИЗ-9).

1000 мм · печать 1:1

Изм.	Кол.уч	Лист	№ док.	Подп.	Дата
Разраб.		Кырлан А.С.			13.11.26
Пров.					
ГИП					
Н. контр.					
Утв.					

ГД-2026-003-АИ

Трёхкомнатная квартира

Общая площадь 78,95* м² · * размеры со скана, не замерены (реестр — л. 6–11, К-13)

Дизайн-проект интерьера трёхкомнатной квартиры

Стадия	Лист	Листов
РП	65	132

Раскладка плитки. Санузел 2. Развёртки стен

М 1:25

Кырлан Александр Сергеевич

выпуск 13.11.2026 № 6f3a8abb2c · стр. 71 из 157

07

Полы и отделка

Кырлан Александр Сергеевич


выпуск 13.11.2026 · 6f3a8abb2c · стр. 72 из 157

План полов

Покрытия, направление укладки, отметки чистого пола, стыки · размеры в мм · отметки в м

Отметки по высоте

±0,000	чистый пол пом. 1, 3–6, 8; отсчёт высот
−0,015	чистый пол пом. 2, 7, ниже на 15 мм
−0,064*	верх плиты — расчёт, не замер (К-13)
сущ. пол	снимается до плиты; не замерен (К-13)

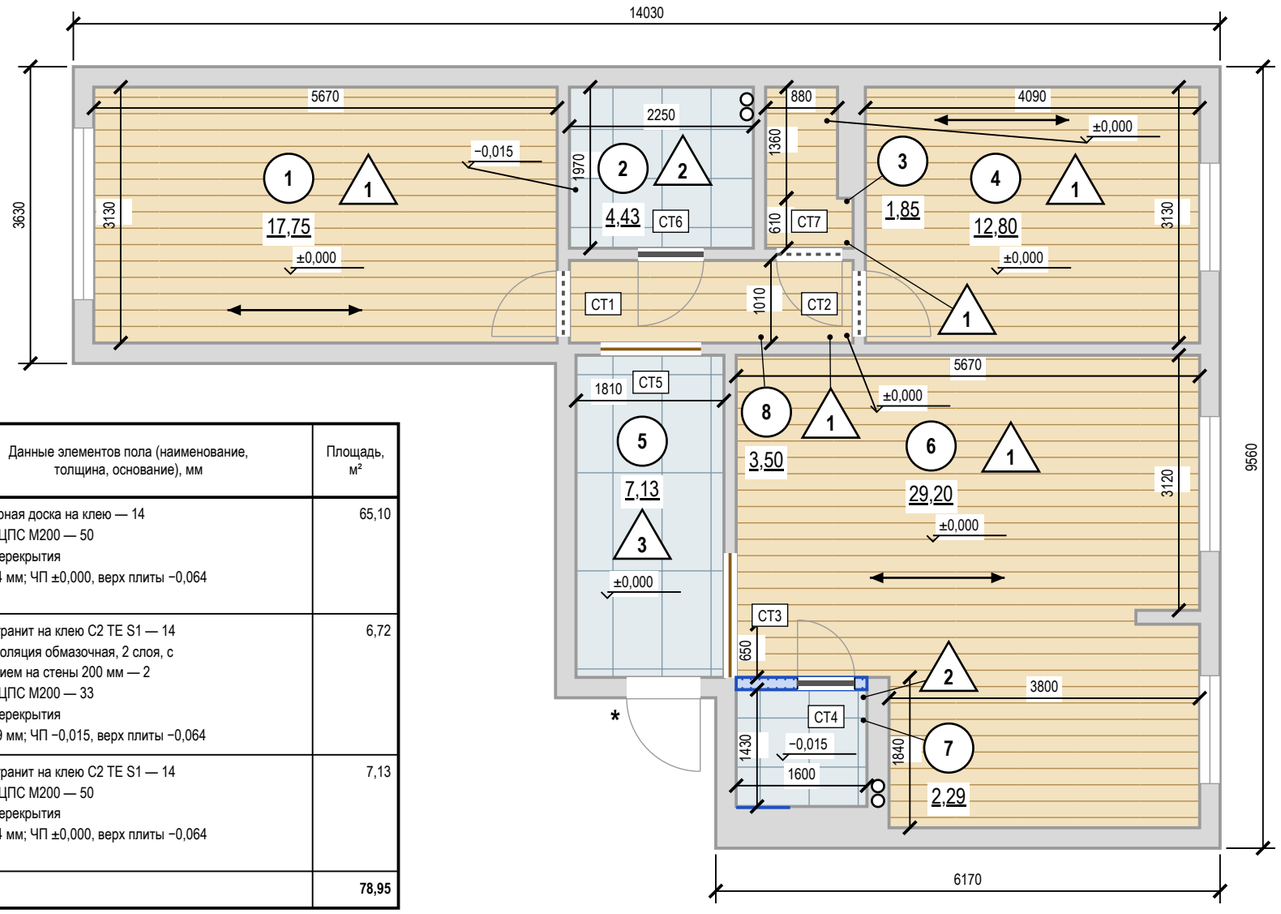

Условные обозначения

- тип 1 — инженерная доска, линии — вдоль доски
- тип 2 — керамогранит 600×600, сетка — формат плитки
- тип 3 — керамогранит 600×1200, сетка — формат плитки
- номер типа пола (экспликация полов)
- схема пола, без масштаба: плита — штриховка, стяжка — точки, звукоизоляция — зигзаг, гидроизоляция — утолщённая линия с заведением на стену
- направление укладки (длинная сторона доски)
- отметка чистого пола, м
- стык в проёме: без порога (б/п)
- стык в проёме: Т-профиль по оси полотна
- стык в проёме: порог
- CT1 — марка стыка (ведомость стыков)
- стояк: К1 — канализация, В1 ХВС, Т3 — ГВС
- новое — возводится по проекту (синим)
- (1) — номер помещения, площадь м²

Экспликация полов

Номер помещения	Тип пола	Схема пола	Данные элементов пола (наименование, толщина, основание), мм	Площадь, м²
1, 3, 4, 6, 8	1		Инженерная доска на клею — 14 Стяжка ЦПС М200 — 50 Плита перекрытия Всего 64 мм; ЧП ±0,000, верх плиты −0,064	65,10
2, 7	2		Керамогранит на клею С2 ТЕ S1 — 14 Гидроизоляция обмазочная, 2 слоя, с заведением на стены 200 мм — 2 Стяжка ЦПС М200 — 33 Плита перекрытия Всего 49 мм; ЧП −0,015, верх плиты −0,064	6,72
5	3		Керамогранит на клею С2 ТЕ S1 — 14 Стяжка ЦПС М200 — 50 Плита перекрытия Всего 64 мм; ЧП ±0,000, верх плиты −0,064	7,13
			Итого	**78,95**

Раскладка покрытий

Пом.	Укладка	Старт (оси от чистовых стен), мм	Отступ 1-го ряда / крайние плитки, мм
1	вдоль стен А/В, прямая	от стены А, 1-й ряд вдоль неё	зазор от стены не задан
2	прямая, сетка 600×600, шов 2	ось X 1101 от Г; ось Y 961 от А	X 498 / 498; Y 358 / 358
3	вдоль стен А/В, прямая	от стены А, 1-й ряд вдоль неё	зазор от стены не задан
4	вдоль стен А/В, прямая	от стены А, 1-й ряд вдоль неё	зазор от стены не задан
5	плитка	раскладка плиточника не задана	
6	вдоль стен А/В, прямая	от стены А, 1-й ряд вдоль неё	зазор от стены не задан
7	прямая, сетка 600×600, шов 2	ось X 776 от Г; ось Y 691 от А	X 474 / 474; Y 389 / 389
8	вдоль стен А/В, прямая	от стены А, 1-й ряд вдоль неё	зазор от стены не задан

Стыки покрытий в проёмах

Марка	Проём	Типы пола	Отметки ЧП	Решение
CT1	1–8 (Д-2)	1 / 1	±0,000 / ±0,000	б/п
CT2	4–8 (Д-2)	1 / 1	±0,000 / ±0,000	б/п
CT3	5–6	3 / 1	±0,000 / ±0,000	Т-профиль
CT4	6–7 (Д-5)	1 / 2	±0,000 / −0,015	порог h=15 мм
CT5	8–5	1 / 3	±0,000 / ±0,000	Т-профиль
CT6	8–2 (Д-3)	1 / 2	±0,000 / −0,015	порог h=15 мм
CT7	8–3 (Д-4)	1 / 1	±0,000 / ±0,000	б/п

Допущения и предложения на листе. Знак «*» принято (замерить): дверь пом. 8 (стена А), Ст К1-1, Ст В1-1, Ст К1-2, Ст В1-2, отметка существующего пола. Знак «**» предложено (согласовать): пол пом. 1–8, плинтус пом. 1, 3–6, 8, стены пом. 2, 7, фартук пом. 6, дверь пом. 6 (стена В), П-1, П-2. См. лист открытых вопросов (листы 6–11).

Примечания

1. За отметку ±0,000 принят чистый пол, не существующий (блок отметок). Площади — по чистым размерам помещений, м²; размеры — в мм.
2. Стык разнотипных покрытий — по оси дверного полотна (под полотном в закрытом положении); решение стыка — по ведомости стыков.
3. Размеры помещений в свету (ширина × длина, мм), не поместившиеся на плане: пом. 3 — 880 × 1360, 1070 × 610; пом. 5 — 1810 × 3940; пом. 6 5670 × 3120, 4890 × 170, 5670 × 650, 3800 × 1840; пом. 8 — 3470 × 1010.
4. Пол санузлов ниже смежных помещений на 15 мм за счёт меньшей толщины стяжки (верх плиты общий — по экспликации полов); гидроизоляция по стяжке с заведением на стены не менее 200 мм (СП 29.13330.2011, п. 7.2), до облицовки — тест проливом и акт скрытых работ.
5. Трубопроводы в конструкции пола не прокладываются: пирог пола 49–64 мм не вмещает выпуски канализации с уклоном — выпуски К1 ведутся по стенам над чистым полом в коробах (лист 49).
6. Звукоизоляционный слой под стяжкой проектом не предусмотрен (стяжка по плите): приведённый уровень ударного шума перекрытия с полом Lnw не более 60 дБ (СП 51.13330.2011, табл. 2) подтвердить по данным дома; при превышении — плавающая стяжка по звукоизоляции с демпферной лентой по контуру и у стояков, пирог пересчитать.
7. Штучные покрытия (инженерная доска): направление — по стрелке; влажность основания по СМ не более 2,0 % (по ТУ изготовителя).
8. Ровность основания — просвет под 2-метровой рейкой не более 2 мм: пом. 1, 3, 4, 6, 8 (инженерная доска), пом. 2, 5, 7 (керамогранит); проверить до укладки покрытия (СП 71.13330.2017, табл. 8.5).
9. Сетка на плитке — условная, в размер формата; точка старта и раскладка — по листу раскладки плитки.
10. Узор покрытия (заливка-код типа пола) прерывается под надписями — площадями помещений и отметками чистого пола.
11. Пироги полов — по экспликации полов: слои сверху вниз, толщины в мм; гидроизоляция мокрых зон — в пироге и в ведомости отделки; схема пола — без масштаба.

1000 мм · печать 1:1

Изм.	Кол.уч	Лист	№ док.	Подп.	Дата
Разраб.		Кырлан А.С.			13.11.26
Пров.					
ГИП					
Н. контр.					
Утв.					

ГД-2026-003-АИ

Трёхкомнатная квартира

Общая площадь 78,95* м² · * размеры со скана, не замерены (реестр — л. 6–11, К-13)

Дизайн-проект интерьера трёхкомнатной квартиры

Стадия	Лист	Листов
РП	66	132

План полов

М 1:75

Кырлан Александр Сергеевич

выпуск 13.11.2026 № 6f3a8abb2c · стр. 73 из 157

Ведомость отделки помещений. Лист 1 из 2

Потолки, стены, низ стен, полы · площади в м², длины в м · отметки в м

Ведомость отделки помещений (форма 1 прил. А ГОСТ 21.501-2018). Лист 1 из 2

№	Наименование помещения	Потолок			Стены и перегородки			Низ стен (плинтус)			Пол		Примечание
		Вид отделки	Код цвета	S, м²	Вид отделки	Код цвета	S, м²	Вид отделки	Код цвета	L, м	Вид отделки	S, м²	
1	Спальня 1 17,75 м²	ГКЛ по каркасу П113, отм. +2,500; +2,600; окраска, Tikkurila Anti-Reflex 2, глубокоматовая, 2 слоя, подготовка Q3	Tikkurila V503	17,75	Окраска, Farrow & Ball Modern Emulsion, матовая, 2 слоя, подготовка Q3 Акцент — стена А: окраска, Farrow & Ball Modern Emulsion, матовая, 2 слоя, подготовка Q3	Farrow & Ball No. 241 Farrow & Ball No. 30	25,00 14,18	Плинтус МДФ h=80 мм, аналог: МДФ под покраску 80×16	Farrow & Ball No. 241	16,8	Аналог: инженерная доска, дуб натуральный, масло, 1-полосная, 14/4 мм, на клею; тип 1, отм. ЧП ±0,000	17,75	Н стен 2500 (до потолка); плинтус в цвет: стены
2	Ванная 4,43 м²	ГКЛВ по каркасу П113, отм. +2,389; окраска, Tikkurila Luja 7, матовая, 2 слоя, подготовка Q3	Tikkurila V503	4,43	Облицовка плиткой, аналог: керамогранит под травертин, матовый, 600×1200×9 мм, клей C2 TE S1, затирка CG2WA	по артикулу	18,61	нет			Аналог: керамогранит ректифицированный под травертин, матовый, 600×600×9 мм; тип 2, отм. ЧП −0,015	4,43	Н стен 2404 (до потолка); гидроизоляция обмазочная, 2 слоя, с заведением на стены 200 мм; над ванной — до 2000 и 300 мм за борт (по пирогу пола); тест проливом и акт скрытых работ
3	Гардеробная 1,85 м²	Существующий потолок, отм. +2,700; окраска, Tikkurila Anti-Reflex 2, глубокоматовая, 2 слоя, подготовка Q3	Tikkurila V503	1,85	Окраска, Tikkurila Harmony, матовая, 2 слоя, подготовка Q3	Tikkurila V503	14,74	Плинтус МДФ h=80 мм, аналог: МДФ под покраску 80×16	Tikkurila V503	5,3	Аналог: инженерная доска, дуб натуральный, масло, 1-полосная, 14/4 мм, на клею; тип 1, отм. ЧП ±0,000	1,85	Н стен 2700 (до потолка); плинтус в цвет: стены
4	Спальня 2 12,80 м²	ГКЛ по каркасу П113, отм. +2,500; +2,600; окраска, Tikkurila Anti-Reflex 2, глубокоматовая, 2 слоя, подготовка Q3	Tikkurila V503	12,80	Окраска, Farrow & Ball Modern Emulsion, матовая, 2 слоя, подготовка Q3 Акцент — стена А: окраска, Farrow & Ball Modern Emulsion, матовая, 2 слоя, подготовка Q3	Farrow & Ball No. 241 Farrow & Ball No. 30	22,21 10,22	Плинтус МДФ h=80 мм, аналог: МДФ под покраску 80×16	Farrow & Ball No. 241	13,6	Аналог: инженерная доска, дуб натуральный, масло, 1-полосная, 14/4 мм, на клею; тип 1, отм. ЧП ±0,000	12,80	Н стен 2500 (до потолка); плинтус в цвет: стены

Примечания

1. Ведомость продолжена на листе 2 из 2; итоги, сводка площадей и примечания — на последнем листе ведомости.

Допущения и предложения на листе

Основа листа: размеры сняты со скана плана заказчика по размерным цепочкам, контрольный обмер на объекте не выполнялся (К-13); высота потолка 2700 мм принята: на плане заказчика не указана (К-11); толщины стен приняты: наружные 250 мм, перегородки 150 мм (на плане 85–190 мм) (К-13); разрешённая мощность 15 кВт принята по типовой квартире, технических условий нет (К-14); утолщение стены 190 × 1360 мм и элемент 1470 × 160 мм плана заказчика не определены (К-12); ниши санузла 2 закрыты перегородкой и фальш-стеной: проектное решение, на плане заказчика ниша у входа открыта (К-18); несущие стены не определены: до технического заключения все существующие стены считаются несущими (К-20); окна существующие и сохраняются; подоконная доска и глубина откосов не заданы — приняты, не замерены (К-27); подрайон климата не задан — принят не северный (жилые от 2,5 м) (К-29).

Знак «**» — предложение проектировщика, заказчиком не утверждено (согласовать с заказчиком): ИЗ-2, К-2, К-23: пол пом. 2, 7 — пирог пола: стяжка 33 мм и обмазочная гидроизоляция добавлены разработчиком проекта; артикул изделия не выбран: позиция описана характеристиками («аналог по характеристикам»), артикул выбирается при закупке; К-2, К-23: стены пом. 2, 7 — артикул изделия не выбран: позиция описана характеристиками («аналог по характеристикам»), артикул выбирается при закупке; К-23: пол пом. 1, 3–6, 8, плинтус пом. 1, 3–6, 8, фартук пом. 6 — артикул изделия не выбран: позиция описана характеристиками («аналог по характеристикам»), артикул выбирается при закупке.

Открытые вопросы и конфликты по листу: К-23.

См. лист открытых вопросов (лист 6, запись К-2; лист 7, записи К-11–К-14, К-18, К-20; лист 8, записи К-23, К-27, К-29; лист 9, запись ИЗ-2).

						ГД-2026-003-АИ
						Трёхкомнатная квартира
						Общая площадь 78,95* м² · * размеры со скана, не замерены (реестр — л. 6–11, К-13)
Изм.	Кол.уч	Лист	№ док.	Подп.	Дата	Дизайн-проект интерьера трёхкомнатной квартиры
Разраб.		Кырлан А.С.			13.11.26	Стадия: РП · Лист: 67 · Листов: 132
Пров.						
ГИП						
Н. контр.						**Ведомость отделки помещений. Лист 1 из 2** · М б/м
Утв.						**Кырлан Александр Сергеевич**

Ведомость отделки помещений. Лист 2 из 2

Потолки, стены, низ стен, полы · площади в м², длины в м · отметки в м

Ведомость отделки помещений (форма 1 прил. А ГОСТ 21.501-2018). Лист 2 из 2

№	Наименование помещения	Потолок			Стены и перегородки			Низ стен (плинтус)			Пол		Примечание
		Вид отделки	Код цвета	S, м²	Вид отделки	Код цвета	S, м²	Вид отделки	Код цвета	L, м	Вид отделки	S, м²	
5	Прихожая 7,13 м²	ГКЛ по каркасу П113, отм. +2,620; окраска, Tikkurila Anti-Reflex 2, глубокоматовая, 2 слоя, подготовка Q3	Tikkurila V503	7,13	Окраска, Farrow & Ball Modern Emulsion, матовая, 2 слоя, подготовка Q3	Farrow & Ball No. 241	21,86	Плинтус МДФ h=80 мм, аналог: МДФ под покраску 80×16	Farrow & Ball No. 241	7,8	Аналог: керамогранит ректифицированный под травертин, матовый, 600×1200×9 мм; тип 3, отм. ЧП ±0,000	7,13	Н стен 2620 (до потолка); плинтус в цвет: стены
6	Кухня-гостиная 29,20 м²	ГКЛ по каркасу П113, отм. +2,500; +2,600; окраска, Tikkurila Anti-Reflex 2, глубокоматовая, 2 слоя, подготовка Q3	Tikkurila V503	29,20	Окраска, Farrow & Ball Modern Emulsion, матовая, 2 слоя, подготовка Q3 Акцент — стена А: окраска, Farrow & Ball Modern Emulsion, матовая, 2 слоя, подготовка Q3 Фартук кухни (стена В): облицовка керамогранитом, аналог: керамогранит под травертин, матовый, 1200×600×9 мм, клей C2 TE S1, затирка CG2WA	Farrow & Ball No. 241 Farrow & Ball No. 30 по артикулу	35,53 14,18 1,85	Плинтус МДФ h=80 мм, аналог: МДФ под покраску 80×16	Farrow & Ball No. 241	22,2	Аналог: инженерная доска, дуб натуральный, масло, 1-полосная, 14/4 мм, на клею; тип 1, отм. ЧП ±0,000	29,20	Н стен 2500 (до потолка); плинтус в цвет: стены
7	Санузел 2 2,29 м²	ГКЛВ по каркасу П113, отм. +2,389; окраска, Tikkurila Luja 7, матовая, 2 слоя, подготовка Q3	Tikkurila V503	2,29	Облицовка плиткой, аналог: керамогранит под травертин, матовый, 600×1200×9 мм, клей C2 TE S1, затирка CG2WA	по артикулу	13,10	нет			Аналог: керамогранит ректифицированный под травертин, матовый, 600×600×9 мм; тип 2, отм. ЧП −0,015	2,29	Н стен 2404 (до потолка); гидроизоляция обмазочная, 2 слоя, с заведением на стены 200 мм; у душа — до 2000 и 500 мм за поддон (по пирогу пола); тест проливом и акт скрытых работ
8	Коридор 3,50 м²	ГКЛ по каркасу П113, отм. +2,620; окраска, Tikkurila Anti-Reflex 2, глубокоматовая, 2 слоя, подготовка Q3	Tikkurila V503	3,50	Окраска, Farrow & Ball Modern Emulsion, матовая, 2 слоя, подготовка Q3	Farrow & Ball No. 241	14,17	Плинтус МДФ h=80 мм, аналог: МДФ под покраску 80×16	Farrow & Ball No. 241	4,5	Аналог: инженерная доска, дуб натуральный, масло, 1-полосная, 14/4 мм, на клею; тип 1, отм. ЧП ±0,000	3,50	Н стен 2620 (до потолка); плинтус в цвет: стены
	Итого			**78,95**			**205,64**			**70,3**		**78,95**	

Сводка площадей по материалам отделки

Поверхность	Материал / код цвета	Серия	Площадь, м²
Потолок	Tikkurila V503	Anti-Reflex 2	72,23
Потолок	Tikkurila V503	Luja 7	6,72
Стены	Farrow & Ball No. 241	Modern Emulsion	118,77
Стены	Farrow & Ball No. 30	Modern Emulsion	38,58
Стены	облицовка плиткой 600×1200×9 мм	аналог: керамогранит под травертин, матовый	31,71
Стены	Tikkurila V503	Harmony	14,74
Фартук	облицовка керамогранитом 1200×600×9 мм	аналог: керамогранит под травертин, матовый	1,85

Допущения и предложения на листе

Основа листа: размеры сняты со скана плана заказчика по размерным цепочкам, контрольный обмер на объекте не выполнялся (К-13); высота потолка 2700 мм принята: на плане заказчика не указана (К-11); толщины стен приняты: наружные 250 мм, перегородки 150 мм (на плане 85–190 мм) (К-13); разрешённая мощность 15 кВт принята по типовой квартире, технических условий нет (К-14); утолщение стены 190 × 1360 мм и элемент 1470 × 160 мм плана заказчика не определены (К-12); ниши санузла 2 закрыты перегородкой и фальш-стеной: проектное решение, на плане заказчика ниша у входа открыта (К-18); несущие стены не определены: до технического заключения все существующие стены считаются несущими (К-20); окна существующие и сохраняются; подоконная доска и глубина откосов не заданы — приняты, не замерены (К-27); подрайон климата не задан — принят не северный (жилые от 2,5 м) (К-29).

Знак «**» — предложение проектировщика, заказчиком не утверждено (согласовать с заказчиком): ИЗ-2, К-2, К-23: пол пом. 2, 7 — пирог пола: стяжка 33 мм и обмазочная гидроизоляция добавлены разработчиком проекта; артикул изделия не выбран: позиция описана характеристиками («аналог по характеристикам»), артикул выбирается при закупке; К-2, К-23: стены пом. 2, 7 — артикул изделия не выбран: позиция описана характеристиками («аналог по характеристикам»), артикул выбирается при закупке; К-23: пол пом. 1, 3–6, 8, плинтус пом. 1, 3–6, 8, фартук пом. 6 — артикул изделия не выбран: позиция описана характеристиками («аналог по характеристикам»), артикул выбирается при закупке.

См. лист открытых вопросов (лист 6, запись К-2; лист 7, записи К-11–К-14, К-18, К-20; лист 8, записи К-23, К-27, К-29; лист 9, запись ИЗ-2).

Примечания

1. Площади поверхностей — по чистым граням стен до отделки: стены = периметр × высоту от чистого пола помещения до низа потолка минус проёмы (облицовка плиткой — до верха облицовки); плинтус = периметр минус дверные проёмы; пол и потолок — по площади помещения. Количество плиток по раскладке. Площади помещений — с учётом всех частей помещения; откосы в площадь стен не входят.
2. Акцентные стены и фартук — отдельными строками, их площадь вычтена из основной отделки стен помещения; фартук — над нижними модулями кухни от столешницы до низа навесных шкафов, где шкафов нет — на 600 мм.
3. Плинтус — длина по периметру за вычетом дверных проёмов; примыкания к наличникам и встроенной мебели — по развёрткам.
4. Формат плитки — Ш×В×Т (ширина × высота в положении укладки × толщина), мм; на полу — вдоль стен А/В × вдоль стен Б/Г.
5. Коды цвета — по веерам производителей; колеровка каждой краски одной партией, проверка выкраса при свете D65 и при лампах проекта.
6. Уровни подготовки Q1–Q4 — система Knauf, не норма ГОСТ/СП; допуски поверхностей — по СП 71.13330.2017 (действующая редакция).
7. «аналог:» — изделие задано характеристиками, марку и артикул согласовать с заказчиком до закупки.
8. Помещения 5, 6, 8: матовая моющаяся, класс 1 EN 13300 — осознанно вместо полуматовой.

						ГД-2026-003-АИ
						Трёхкомнатная квартира Общая площадь 78,95* м² · * размеры со скана, не замерены (реестр — л. 6–11, К-13)
Изм.	Кол.уч	Лист	№ док.	Подп.	Дата	
Разраб.		Кырлан А.С.			13.11.26	Дизайн-проект интерьера трёхкомнатной квартиры
Пров.						
ГИП						
Н. контр.						**Ведомость отделки помещений. Лист 2 из 2** М б/м
Утв.						

Стадия	Лист	Листов
РП	68	132

Кырлан Александр Сергеевич

Колерная карта

Цвета и материалы по помещениям · палитра проекта · выкрасы на согласование

Колерная карта по помещениям

Помещение	Поверхность	Образец	Поз.	Система и код цвета	Производитель, линейка / материал, артикул	Блеск	Класс истирания	LRV	Площадь
1. Спальня 1 17,75 м²	стены		**К1**	Farrow & Ball No. 241	Farrow & Ball · Modern Emulsion	матовая	1	67	25,0 м²
	акцент А		**К2**	Farrow & Ball No. 30	Farrow & Ball · Modern Emulsion	матовая	1	7	14,2 м²
	потолок		**К3**	Tikkurila V503	Tikkurila · Anti-Reflex 2	глубокомат.	2	86	17,8 м²
	пол		**КМ1**	по образцу	инженерная доска · аналог по хар.				17,8 м²
	плинтус		**К4**	Farrow & Ball No. 241	МДФ · в цвет Farrow & Ball			67	16,8 м
2. Ванная 4,43 м²	стены		**КМ2**	по образцу	плитка · аналог по хар.				18,6 м²
	потолок		**К5**	Tikkurila V503	Tikkurila · Luja 7	матовая	1	86	4,4 м²
	пол		**КМ3**	по образцу	керамогранит · аналог по хар.				4,4 м²
3. Гардеробная 1,85 м²	стены		**К6**	Tikkurila V503	Tikkurila · Harmony	матовая	1	86	14,7 м²
	потолок		**К3**	Tikkurila V503	Tikkurila · Anti-Reflex 2	глубокомат.	2	86	1,9 м²
	пол		**КМ1**	по образцу	инженерная доска · аналог по хар.				1,9 м²
	плинтус		**К7**	Tikkurila V503	МДФ · в цвет Tikkurila			86	5,3 м
4. Спальня 2 12,8 м²	стены		**К1**	Farrow & Ball No. 241	Farrow & Ball · Modern Emulsion	матовая	1	67	22,2 м²
	акцент А		**К2**	Farrow & Ball No. 30	Farrow & Ball · Modern Emulsion	матовая	1	7	10,2 м²
	потолок		**К3**	Tikkurila V503	Tikkurila · Anti-Reflex 2	глубокомат.	2	86	12,8 м²
	пол		**КМ1**	по образцу	инженерная доска · аналог по хар.				12,8 м²
	плинтус		**К4**	Farrow & Ball No. 241	МДФ · в цвет Farrow & Ball			67	13,6 м
5. Прихожая 7,13 м²	стены		**К1**	Farrow & Ball No. 241	Farrow & Ball · Modern Emulsion	матовая	1	67	21,9 м²
	потолок		**К3**	Tikkurila V503	Tikkurila · Anti-Reflex 2	глубокомат.	2	86	7,1 м²
	пол		**КМ4**	по образцу	керамогранит · аналог по хар.				7,1 м²
	плинтус		**К4**	Farrow & Ball No. 241	МДФ · в цвет Farrow & Ball			67	7,8 м
6. Кухня-гостиная 29,2 м²	стены		**К1**	Farrow & Ball No. 241	Farrow & Ball · Modern Emulsion	матовая	1	67	35,5 м²
	акцент А		**К2**	Farrow & Ball No. 30	Farrow & Ball · Modern Emulsion	матовая	1	7	14,2 м²
	потолок		**К3**	Tikkurila V503	Tikkurila · Anti-Reflex 2	глубокомат.	2	86	29,2 м²
	пол		**КМ1**	по образцу	инженерная доска · аналог по хар.				29,2 м²
	плинтус		**К4**	Farrow & Ball No. 241	МДФ · в цвет Farrow & Ball			67	22,2 м
	фартук		**КМ5**	по образцу	керамогранит · аналог по хар.				1,9 м²
7. Санузел 2 2,29 м²	стены		**КМ2**	по образцу	плитка · аналог по хар.				13,1 м²
	потолок		**К5**	Tikkurila V503	Tikkurila · Luja 7	матовая	1	86	2,3 м²
	пол		**КМ3**	по образцу	керамогранит · аналог по хар.				2,3 м²
8. Коридор 3,5 м²	стены		**К1**	Farrow & Ball No. 241	Farrow & Ball · Modern Emulsion	матовая	1	67	14,2 м²
	потолок		**К3**	Tikkurila V503	Tikkurila · Anti-Reflex 2	глубокомат.	2	86	3,5 м²
	пол		**КМ1**	по образцу	инженерная доска · аналог по хар.				3,5 м²
	плинтус		**К4**	Farrow & Ball No. 241	МДФ · в цвет Farrow & Ball			67	4,5 м

Перечень выкрасов на согласование

№	Код	Бренд / веер	Пом. / стена	Подложка	Формат	Статус
1	No. 241	Farrow & Ball	1, 4, 5, 6, 8	ГКЛ с грунтом; МДФ под эмаль	600×1000; 300×600	к выполнению
2	No. 30	Farrow & Ball	1 А, 4 А, 6 А	ГКЛ с грунтом	600×1000	к выполнению
3	V503	Tikkurila	1, 2, 3, 4, 5, 6, 7, 8	ГКЛ с грунтом; МДФ под эмаль	600×1000; 300×600	к выполнению

Примечания

1. Цвет на листе и на экране — ориентир. До покраски — выкрас на объекте: не меньше А3 (или лист ГКЛ), на грунте под эту краску, не на белой шпаклёвке, в 2 слоя; на обороте — код, бренд, веер, дата. Смотреть днём и вечером, рядом с образцами пола и плитки; к основному цвету стен — ещё 2 соседних оттенка. Красить только в цвет утверждённого выкраса.
2. Краску заказывать по коду из графы «Система и код цвета» у бренда этого кода, не «аналогом» другого; весь объём одного кода — одной партией, колеруемую краску — за один проход машины.
3. Площади — те же, что в ведомости отделки (лист 67); сколько краски заказать — в спецификации отделочных материалов (лист 70).

Допущения и предложения на листе. Основа листа: размеры сняты со скана плана заказчика по размерным цепочкам, контрольный обмер на объекте не выполнялся (К-13); высота потолка 2700 мм принята: на плане заказчика не указана (К-11); толщины стен приняты: наружные 250 мм, перегородки 150 мм (на плане 85–190 мм) (К-13); разрешённая мощность 15 кВт принята по типовой квартире, технических условий нет (К-14); утолщение стены 190 × 1360 мм и элемент 1470 × 160 мм плана заказчика не определены (К-12); ниши санузла 2 закрыты перегородкой и фальш-стеной: проектное решение, на плане заказчика ниша у входа открыта (К-18); несущие стены не определены: до технического заключения все существующие стены считаются несущими (К-20); окна существующие и сохраняются; подоконная доска и глубина откосов не заданы — приняты, не замерены (К-27); подрайон климата не задан — принят не северный (жилые от 2,5 м) (К-29). Знак «**» — предложено, не утверждено (согласовать): ИЗ-2, К-2, К-23: пол пом. 2, 7; К-2, К-23: стены пом. 2, 7; К-23: пол пом. 1, 3–6, 8, плинтус пом. 1, 3–6, 8, фартук пом. 6. См. лист открытых вопросов (лист 6, записи К-2, К-3; лист 7, записи К-11–К-14, К-18, К-20; лист 8, записи К-23, К-27, К-29; лист 9, запись ИЗ-2; лист 11, запись ИЗ-20).

Схема квартиры: цвет стен и акценты (б/м)



Схема палитры проекта

Стиль: Современный (контемпорари) · схема: аналоговая

основной	основной	второстепенный	акцентный
Tikkurila V503	**Farrow & Ball No. 241**	**Tikkurila H487**	**Farrow & Ball No. 30**
Winter LRV 86 потолок 1,2,3,4,5,6,7,8; стены 3; плинтус 3; текстиль/декор 1,2,4,6,7	Skimming Stone LRV 67 стены 1,4,5,6,8; плинтус 1,4,5,6,8	Pumice LRV 57 текстиль/декор 1,2,4,6	Hague Blue LRV 7 акцент 1,4,6; текстиль/декор 1,4,6

План 60/30/10

60%	30%	10%

Окраска, факт — по площади стен, акцентов, потолков

85%	15%

окрашено всего 251 м²; второстепенный тон несут мебель и текстиль

Текстиль и декор в цветах вне палитры проекта

- NCS S 3005-Y20R тёплый тауп-серый — пом. 1 (Т3)
- Farrow & Ball No. 47 Green Smoke — пом. 2 (Т20**, ДК10**), 4 (Т11, ДК19**), 7 (Т23**)
- Tikkurila V484 Driftwood — пом. 4 (Т9), 5 (Т25**), 6 (Т15, Т16, Т19)
- Farrow & Ball No. 229 Elephant's Breath — пом. 4 (Т10), 6 (ДК25**), 7 (ДК12**)

Условные обозначения

- **К1** Farrow & Ball No. 241 · Skimming Stone · Modern Emulsion · матовая · кл. 1
- **К2** Farrow & Ball No. 30 · Hague Blue · Modern Emulsion · матовая · кл. 1
- **К3** Tikkurila V503 · Winter · Anti-Reflex 2 · глубокомат. · кл. 2
- **К4** Farrow & Ball No. 241 · Skimming Stone · МДФ
- **К5** Tikkurila V503 · Winter · Luja 7 · матовая · кл. 1
- **К6** Tikkurila V503 · Winter · Harmony · матовая · кл. 1
- **К7** Tikkurila V503 · Winter · МДФ
- дерево (доска, паркет, ламинат) — рисунок досок
- керамогранит, плитка, камень — сетка швов по формату
- **КМ1** аналог: инженерная доска, дуб натуральный, масло, 1-полосная, 14/4 мм
- **КМ2** плитка · аналог: керамогранит под травертин, матовый, 600×1200×9 мм
- **КМ3** аналог: керамогранит ректифицированный под травертин, матовый, 600×600×9 мм
- **КМ4** аналог: керамогранит ректифицированный под травертин, матовый, 600×1200×9 мм
- **КМ5** аналог: керамогранит под травертин, матовый, 1200×600×9 мм

К — краска, КМ — отделочный материал (тон КМ — по описанию, эталон — образец материала); кл. — класс истирания (1 — самый стойкий к мытью); LRV — светлота цвета: 0 — чёрный, 100 — белый

Изм.	Кол.уч	Лист	№ док.	Подп.	Дата
Разраб.		Кырлан А.С.			13.11.26
Пров.					
ГИП					
Н. контр.					
Утв.					

ГД-2026-003-АИ

Трёхкомнатная квартира

Общая площадь 78,95* м² · * размеры со скана, не замерены (реестр — л. 6–11, К-13)

Дизайн-проект интерьера трёхкомнатной квартиры

Стадия	Лист	Листов
РП	69	132

Колерная карта

М б/м

Кырлан Александр Сергеевич

выпуск 13.11.2026 № 6f3a8abb2c · стр. 76 из 157

Спецификация отделочных материалов

Форма 1 по ГОСТ 21.110-2013 · количества — из геометрии проекта, с запасом

ПРЕДВАРИТЕЛЬНО · не для производства работ · открыто пунктов: 28 (реестр — л. 6–11)

Поз.	Наименование и техническая характеристика	Тип, марка, обозначение документа	Код продукции	Поставщик	Ед. изм.	Кол.	Масса 1 ед., кг	Примечание
	Лакокрасочные материалы							
1	Краска интерьерная водно-дисперсионная акриловая для стен, матовая, класс мокрого истирания 1 по EN 13300, база A; цвет по вееру Farrow & Ball No. 241 «Skimming Stone», колеровка машинная	Farrow & Ball Modern Emulsion		Farrow & Ball	л	32,5		поз. К1 колерной карты; пом. 1, 4, 5, 6, 8; S = 118,8 м² × 2 сл. × 0,12 л/м² = 28,5 л, +10 % и 0,5 л на подкраску → ≥ 31,9 л; тара 6 × 5 л + 1 × 2,5 л
2	Краска интерьерная водно-дисперсионная акриловая для акцентных стен, матовая, класс мокрого истирания 1 по EN 13300, база C; цвет по вееру Farrow & Ball No. 30 «Hague Blue», колеровка машинная	Farrow & Ball Modern Emulsion		Farrow & Ball	л	12,5		поз. К2 колерной карты; пом. 1, 4, 6; S = 38,6 м² × 2 сл. × 0,12 л/м² = 9,3 л, +10 % и 0,5 л на подкраску → ≥ 10,7 л; тара 2 × 5 л + 1 × 2,5 л
3	Краска интерьерная водно-дисперсионная акриловая для потолков, глубокоматовая, класс мокрого истирания 2 по EN 13300, база A; цвет по вееру Tikkurila V503 «Winter», колеровка машинная	Tikkurila Anti-Reflex 2		Tikkurila	л	19,8		поз. К3 колерной карты; пом. 1, 3, 4, 5, 6, 8; S = 72,2 м² × 2 сл. × 0,12 л/м² = 17,3 л, +10 % и 0,5 л на подкраску → ≥ 19,6 л; тара 2 × 9 л + 2 × 0,9 л
4	Краска интерьерная водно-дисперсионная акриловая для потолков, матовая, класс мокрого истирания 1 по EN 13300, база A; цвет по вееру Tikkurila V503 «Winter», колеровка машинная	Tikkurila Luja 7		Tikkurila	л	2,7		поз. К5 колерной карты; пом. 2, 7; S = 6,7 м² × 2 сл. × 0,12 л/м² = 1,6 л, +10 % и 0,5 л на подкраску → ≥ 2,3 л; тара 1 × 2,7 л
5	Краска интерьерная водно-дисперсионная акриловая для стен, матовая, класс мокрого истирания 1 по EN 13300, база A; цвет по вееру Tikkurila V503 «Winter», колеровка машинная	Tikkurila Harmony		Tikkurila	л	4,5		поз. К6 колерной карты; пом. 3; S = 14,7 м² × 2 сл. × 0,12 л/м² = 3,5 л, +10 % и 0,5 л на подкраску → ≥ 4,4 л; тара 1 × 2,7 л + 2 × 0,9 л
6	Краска для МДФ и дерева в цвет Farrow & Ball No. 241 «Skimming Stone» — окраска плинтуса; блеск не ниже блеска стен	марка не задана			л	1,7		поз. К4; пом. 1, 4, 5, 6, 8; L = 65,1 м, S = 6,2 м² × 2 сл. × 0,12 л/м² + 10 %; продукт подобрать в веере Farrow & Ball
7	Краска для МДФ и дерева в цвет Tikkurila V503 «Winter» — окраска плинтуса; блеск не ниже блеска стен	марка не задана			л	0,5		поз. К7; пом. 3; L = 5,3 м, S = 0,5 м² × 2 сл. × 0,12 л/м² + 10 %; продукт подобрать в веере Tikkurila
8	Грунтовка акриловая под окраску стен и потолков — из системы производителя краски	по системе краски			м²	252		площадь окраски стен, акцентов и потолков; 1 слой перед окраской; расход — по ТУ грунтовки
	Плитка и керамогранит							
9	Керамогранит под травертин, 600×600×9 мм, ректификат, водопоглощение 0,1 % (BIa), противоскольжение R10, PEI IV	аналог по характеристикам			м²	9,72		шов 2 мм; Ванная, пол; Санузел 2, пол; по раскладке 24 шт (S = 6,72 м²), с запасом 27 шт
10	Керамогранит под травертин, 600×1200×9 мм, ректификат, водопоглощение 0,1 %	аналог по характеристикам			м²	56,88		шов 2 мм; Ванная, стены А–Г; Ванная, короб стояков Ш1 248×459; Ванная, короб инсталляции; Санузел 2, стены А–Г; Санузел 2, короб инсталляции; по раскладке 67 шт (S = 33,26 м²), с запасом 79 шт
11	Керамогранит ректифицированный под травертин, матовый, 600×1200×9 мм, водопоглощение 0,1 % (BIa), противоскольжение R10, PEI IV	аналог по характеристикам			м²	10,08		шов 2 мм; Прихожая, пол; по раскладке 12 шт (S = 7,13 м²), с запасом 14 шт
12	Керамогранит под травертин, матовый, 1200×600×9 мм, ректификат, водопоглощение 0,1 % (BIa)	аналог по характеристикам			м²	3,60		шов 2 мм; Кухня-гостиная, фартук (ст. В); по раскладке 4 шт (S = 1,85 м²), с запасом 5 шт
	Напольные покрытия							
13	Инженерная доска, дуб натуральный, масло, 1-полосная, 14/4 мм, эмиссия E1, укладка на клей	аналог по характеристикам			м²	70,4		пом. 1, 3, 4, 6, 8; S = 65,78 м² (пол + половина стены в дверных проёмах, как в смете) + 7 %; к заказу — кратно упаковке
14	Клей для паркета и инженерной доски, эластичный (СМП / полиуретановый)	по рекомендации производителя доски			м²	66		площадь приклейки; расход и шпатель — по ТУ клея
	Погонажные изделия							
15	Плинтус МДФ под покраску 80×16, крепление к стене, окраска в цвет Farrow & Ball No. 241	аналог по характеристикам			м	72		пом. 1, 4, 5, 6, 8; L = 65,1 м (периметр без дверных проёмов) + 10 % на подрезку; в штуках — по длине планки
16	Плинтус МДФ под покраску 80×16, крепление к стене, окраска в цвет Tikkurila V503	аналог по характеристикам			м	6		пом. 3; L = 5,3 м (периметр без дверных проёмов) + 10 % на подрезку; в штуках — по длине планки
	Смеси и материалы для облицовки							
17	Затирка для швов плитки, класс CG2WA по EN 13888	Mapei Ultracolor Plus 132		Mapei	кг	3,8		по раскладке (a+b)/(a·b) × шов × t × 1,6 + 10 %; в т. ч. 0,7 кг — позиции раскладки без марки
18	Клей плиточный C2 TE S1 по EN 12004, слой 5 мм	Ceresit CM 17		Ceresit	кг	307		13 меш. по 25 кг; 1,5 кг/м² на 1 мм слоя + 10 %; в т. ч. 59 кг — позиции раскладки без марки
19	Гидроизоляция обмазочная мокрых зон: пол, стены по периметру, зоны замачивания; 2 слоя с армирующей лентой в углах	аналог по характеристикам			м²	20		площадь по листу раскладки плитки + 10 %; расход смеси — по ТУ
20	Лента демпферная по периметру пола из плитки	аналог по характеристикам			м	22,4		периметр без дверных проёмов + 10 %

Примечания

1. Количества — из геометрии проекта: площади поверхностей по чистым граням стен до отделки (те же, что в ведомости отделки и колерной карте), плитка, клей и затирка — по раскладке плиточника; в графе «Кол.» — к заказу, с запасом.
2. Краска: расход 0,12 л/м² на слой в 2 слоя, если по ТУ не задан иной; запас 10 % и 0,5 л на подкраску каждого кода. Один код — одна партия, колеровка машинная в колеровочном центре бренда; в заказ — только после утверждения выкраса (колерная карта). Фасовка — по каталогу бренда на дату выпуска; к заказу — не меньше расчётного объёма.
3. «Аналог по характеристикам» — допускается изделие другого производителя с характеристиками не ниже указанных, по согласованию с автором проекта.
4. Графы «Код продукции» и «Масса 1 ед.» не заполнены: коды по классификатору продукции не присвоены, масса единицы до 25 кг (ГОСТ 21.110-2013).
5. Грунтовка и клей для доски указаны площадью обработки; объём — по ТУ выбранного продукта.

Допущения и предложения на листе. Знак «**» предложено (согласовать): пол пом. 1–8, плинтус пом. 1, 3–6, 8, стены пом. 2, 7, фартук пом. 6. См. лист открытых вопросов (листы 6–11).

Изм.	Кол.уч	Лист	№ док.	Подп.	Дата
Разраб.		Кырлан А.С.			13.11.26
Пров.					
ГИП					
Н. контр.					
Утв.					

ГД-2026-003-АИ

Трёхкомнатная квартира

Общая площадь 78,95* м² · * размеры со скана, не замерены (реестр — л. 6–11, К-13)

Дизайн-проект интерьера трёхкомнатной квартиры

Стадия	Лист	Листов
РП	70	132

Спецификация отделочных материалов

М б/м

Кырлан Александр Сергеевич

выпуск 13.11.2026 · № 6f3a8abb2c · стр. 77 из 157

Концепция декора и визуализации

Современный (контемпорари) · warm contemporary · визуализации, палитра, материалы, ключевые предметы




Визуализация 1. Вид сверху (3D): планировка с мебелью, текстилем и декором

Расстановка — по плану мебели (лист 32); шторы, ковры, картины и растения — по плану текстиля и декора (лист 72).




Визуализация 18. Кухня-гостиная (пом. 6)

шторы Т13, Т14, Т15 · ковёр Т16 · картины ДК6, ДК24** · растение ДК7 · подушки, пледы Т17, Т18, Т19

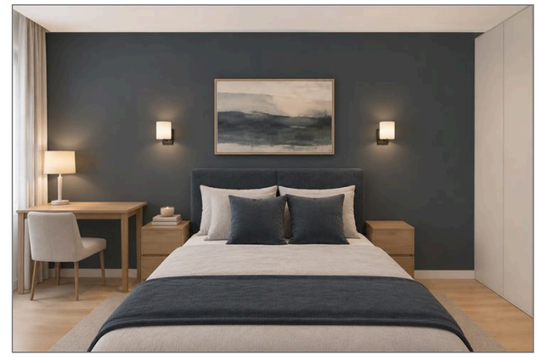

Визуализация 11. Спальня 1 (пом. 1)

шторы Т1, Т2 · ковёр Т3 · картина ДК1 · зеркало ДК15** · растение ДК16** · подушки, пледы Т4, Т5, Т6

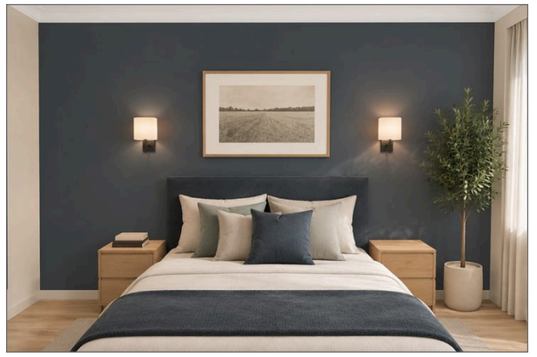

Визуализация 13. Спальня 2 (пом. 4)

шторы Т7, Т8 · ковёр Т9 · картина ДК3 · зеркало ДК4 · растение ДК20** · подушки, пледы Т10, Т11, Т12



Визуализация 8. Ванная (пом. 2)

ковёр Т22** · зеркало ДК2 · подушки, пледы Т20**, Т21**

Материалы и фактуры



Дуб натуральный

пол: пом. 1, 3, 4, 6, 8; рамы ДК1, ДК3, ДК14**, ДК24**



Травертин (керамогранит)

пол и стены санузлов, фартук: пом. 2, 5, 6, 7



Букле

подушки: Т10, Т17



Лён

портьеры, подушки, полотенца: Т1, Т4, Т7, Т13, Т15, Т20**, Т21**, Т23**,



Бронза и чёрный металл

рамы ДК4, ДК5, ДК13**, ДК15** чёрный; фурнитура, светильники

Палитра 60/30/10 и цвета текстиля



- Tikkurila V503 (Winter), LRV 86 — 60 % база — Т2, Т8, Т14, Т21, Т24
- Tikkurila H487 (Pumice), LRV 57 — 30 % второй цвет — Т1, Т4, Т7, Т13, Т17, Т22
- NCS S 3005-Y20R (тёплый тауп-серый), LRV 44 — текстиль — Т3
- Tikkurila V484 (Driftwood), LRV 49 — текстиль — Т9, Т15, Т16, Т19, Т25
- Farrow & Ball No. 241 (Skimming Stone), LRV 67 — 60 % база
- Farrow & Ball No. 30 (Hague Blue), LRV 7 — 10 % акцент — Т5, Т6, Т12, Т18
- Farrow & Ball No. 47 (Green Smoke), LRV 19 — акцент текстиля — Т11, Т20, Т23
- Farrow & Ball No. 229 (Elephant's Breath), LRV 52 — текстиль — Т10

Ключевые предметы

— Диван М2 2600×1000 — кухня-гостиная; подушки и плед Т17, Т18, Т19
— Кровати С1, С7 — над изголовьем картины ДК1, ДК3; текстиль Т4, Т5, Т6, Т10, Т11, Т12
— Ковры Т3, Т9, Т16, Т22**, Т25** — шерсть, хлопок тафтинг, на противоскользящей подложке
— Картины ДК1, ДК3, ДК6, ДК13**, ДК14**, ДК24** — центр на высоте 1500–1650 мм
— Зеркала в рост ДК4, ДК5, ДК15**; над умывальниками ДК2, ДК9
— Шторы-волна Т1, Т7, Т13 (Tikkurila H487), тюль Т2, Т8, Т14 (Tikkurila V503) — в нишах потолка
— Растение ДК16**, ваза ДК10**, растение ДК20**, растение ДК7, ваза ДК8, ваза ДК12**

Настроение

Warm contemporary: потолки V503, стены Skimming Stone No. 241, грейж H487 в текстиле, один глубокий акцент Hague Blue No. 30 (изголовья спален, ТВ-стена). Настроение стиля: актуальность, комфорт, мягкая геометрия, контраст фактур, открытость, уверенность. Свет тёплый, 2700–3000 K.

Примечания

1. Визуализации — образ интерьера. Изделия, размеры, высоты подвеса и привязки — по чертежам (план текстиля и декора — лист 72; шторы и карнизы — лист 73; ведомость текстиля — лист 74; ведомость декора и развеска — лист 75); при расхождении действуют чертежи и ведомости.
2. Коды цвета — ориентир подбора по веерам производителей; ткань утверждается по образцу при дневном свете и при свете проекта 2700–3000 K.
3. Мелкий стайлинг на визуализациях (книги, посуда, свечи) в ведомости не входит и поставляется заказчиком по желанию.

Допущения и предложения на листе. Знак «**» предложено (согласовать). См. лист открытых вопросов (листы 6–11).


						ГД-2026-003-АИ		
						Трёхкомнатная квартира Общая площадь 78,95* м² · * размеры со скана, не замерены (реестр — л. 6–11, К-13)		
Изм.	Кол.уч	Лист	№ док.	Подп.	Дата	Дизайн-проект интерьера трёхкомнатной квартиры	Стадия	Лист	Листов
Разраб.		Кырлан А.С.			13.11.26		РП	71	132
Пров.									
ГИП									
						Концепция декора и визуализации М б/м	Кырлан Александр Сергеевич		
Н. контр.									
Утв.									

выпуск 13.11.2026 № 6f3a8abb2c · стр. 78 из 157

План текстиля и декора

Шторы и карнизы, ковры, картины и зеркала, растения · размеры в мм от чистовых стен и чистого пола · марки — по ведомостям

ПРЕДВАРИТЕЛЬНО · не для производства работ · открыто пунктов: 28 (реестр — л. 6–11)

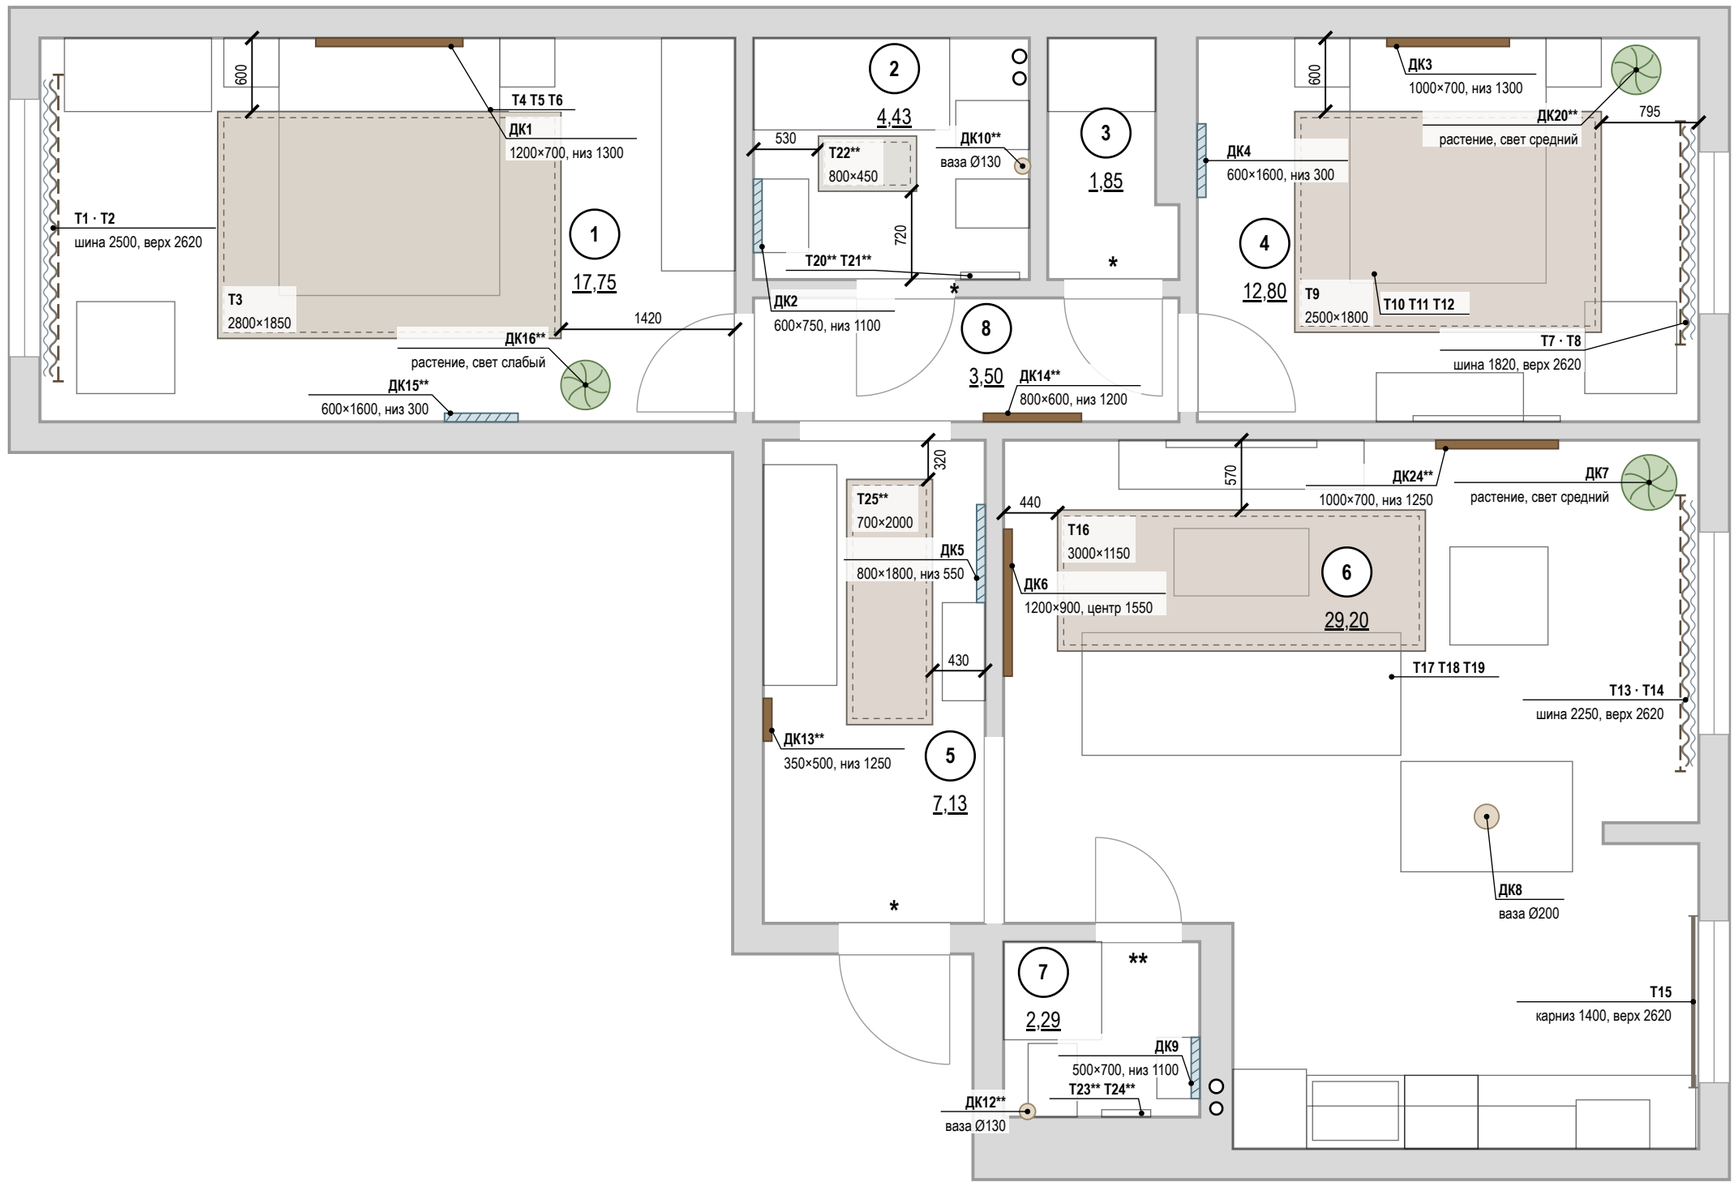

Условные обозначения

- ковёр — габарит в масштабе, цвет изделия
- шина или карниз штор (выше плоскости разреза)
- портьеры (штора-волна)
- тюль (на плане — волнистая линия)
- римская или рулонная штора в проёме
- картина на стене — ширина в масштабе
- зеркало на стене — ширина в масштабе
- растение в кашпо — диаметр в масштабе
- ваза, настольный декор
- подушки, пледы — марка на выноске к своей мебели
- привязка от чистовой стены, мм
- (1) номер помещения, площадь м²
- стены (подложка обмера)
- * «*» — принято, не замерено и не подтверждено
- ** «**» — предложение проектировщика, заказчиком не утверждено

Т1, ДК1 — марки по ведомостям текстиля и декора

Экспликация помещений

лист 27 · на плане — номера в марках

Окна: шина → полотно, мм

Поз.	Шина	Верх шины	Полотно, низ
Т1, Т2	2500	2620, ниша	2610, низ 10
Т7, Т8	1820	2620, ниша	2610, низ 10
Т13, Т14	2250	2620, ниша	2610, низ 10
Т15	1400	2620, ниша	1620, низ 1000

Допущения и предложения на листе. Основа листа: размеры сняты со скана плана заказчика по размерным цепочкам, контрольный обмер на объекте не выполнялся (К-13); высота потолка 2700 мм принята: на плане заказчика не указана (К-11); толщины стен приняты: наружные 250 мм, перегородки 150 мм (на плане 85–190 мм) (К-13); разрешённая мощность 15 кВт принята по типовой квартире, технических условий нет (К-14); утолщение стены 190 × 1360 мм и элемент 1470 × 160 мм плана заказчика не определены (К-12); ниши санузла 2 закрыты перегородкой и фальш-стеной: проектное решение, на плане заказчика ниша у входа открыта (К-18); несущие стены не определены: до технического заключения все существующие стены считаются несущими (К-20); окна существующие и сохраняются; подоконная доска и глубина откосов не заданы — приняты, не замерены (К-27); подрайон климата не задан — принят не северный (жилые от 2,5 м) (К-29). Знак «*» — принято, не замерено и не подтверждено (замерить на объекте): К-17: Ст К1-1, Ст В1-1, Ст К1-2, Ст В1-2. Знак «**» — предложение проектировщика, заказчиком не утверждено (согласовать с заказчиком). См. лист открытых вопросов (лист 7, записи К-11–К-14, К-17, К-18, К-20; лист 8, записи К-25–К-27, К-29; лист 11, запись ИЗ-20); по листу — ИЗ-20.

Примечания

1. Размеры — в мм. Отступы ковров — от чистовых стен; высоты картин и зеркал — от чистого пола до центра или низа рамы.
2. Шторы в пол — на шинах в нишах потолка (ниша — план потолков, лист 59); закладная под шину в нише — до обшивки ГКЛ. Римские шторы — на карнизах в нишах потолка. Схемы окон, длины полотен и сборка — лист 73.
3. Картины и зеркала массой более 5 кг — на анкеры по основанию, нагрузка крепежа не меньше двойной массы изделия; на ГКЛ — только по закладной. Декор не перекрывает розетки и выключатели.
4. Ковры на гладком полу — на противоскользящей подложке.
5. Мебель — по плану расстановки мебели (лист 32); ведомость текстиля — лист 74, ведомость декора и схемы развески — лист 75.
6. Знак «*» у проёма — допущение: положение проёма не замерено (дверь пом. 5, стена В; дверь пом. 8, стена А (2 шт.)); размер напечатан как принятый. Реестр: листы 6–11, вопросы К-26, К-25.
7. Номера помещений — по экспликации (лист 27); наименования и площади на этом листе не дублируются.
8. Марки текстиля «Т» и декора «Д» относятся только к листам текстиля и декора; индексы трубопроводов Т1–Т4 — на листах ВК и ОВ.

1000 мм · печать 1:1

Изм.	Кол.уч	Лист	№ док.	Подп.	Дата
Разраб.		Кырлан А.С.			13.11.26
Пров.					
ГИП					
Н. контр.					
Утв.					

ГД-2026-003-АИ

Трёхкомнатная квартира

Общая площадь 78,95* м² · * размеры со скана, не замерены (реестр — л. 6–11, К-13)

Дизайн-проект интерьера трёхкомнатной квартиры

Стадия	Лист	Листов
РП	72	132

План текстиля и декора

М 1:50

Кырлан Александр Сергеевич

выпуск 13.11.2026 № 6f3a8abb2c · стр. 79 из 157

08

Декор и текстиль


Кырлан Александр Сергеевич

выпуск 13.11.2026 · 6f3a8abb2c · стр. 80 из 157


Шторы и карнизы

Схемы окон «шина → полотно» (М 1:50) · отметки от чистого пола помещения · размеры в мм


Окно 1 — Спальня 1 (пом. 1): Т1, Т2 (М 1:50)

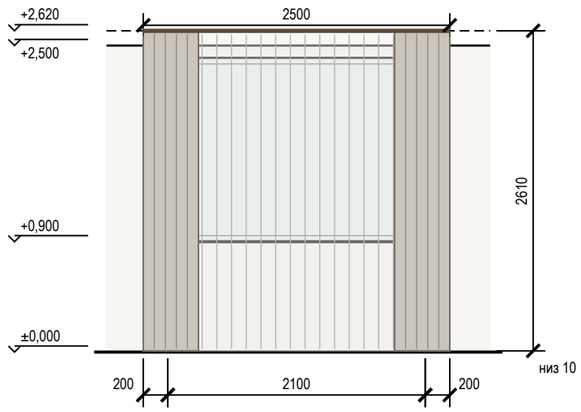


Окно 1 — Спальня 2 (пом. 4): Т7, Т8 (М 1:50)

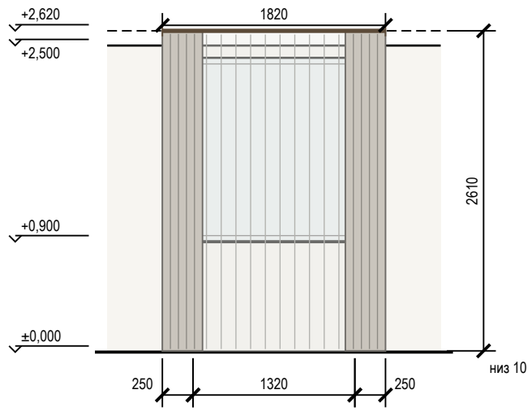

Окно 1 — Кухня-гостиная (пом. 6): Т13, Т14 (М 1:50)

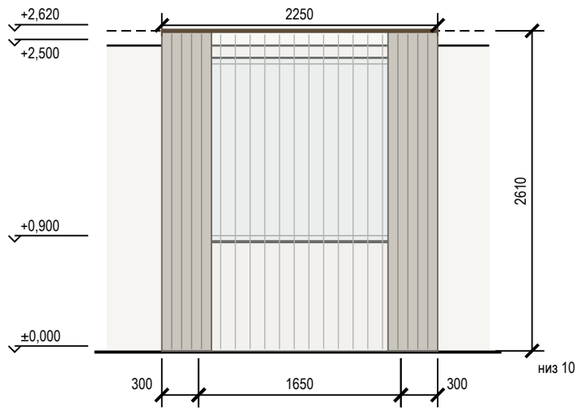

Окно 2 — Кухня-гостиная (пом. 6): Т15 (М 1:50)

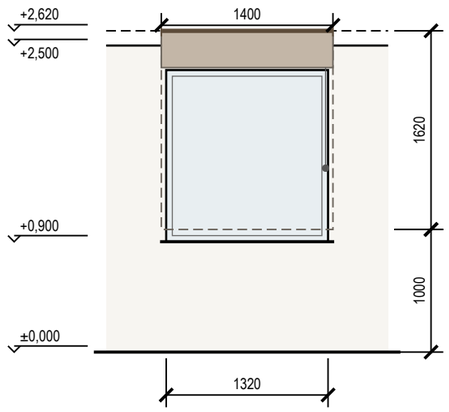

Карта окон: окно → шина → полотно

Поз.	Окно, пом.	Проём Ш×В, подоконник	Верх ниши	Изделие	Шина / карниз: длина, крепление	Верх шины	Полотно: длина, низ	Управление
Т1	1, пом. 1	2100×1500, подок. 900	+2,620	портьеры	шина, 2500, в нише потолка, вынос 150	+2,620	2610, низ 10 (парит)	вручную
Т2	1, пом. 1	2100×1500, подок. 900	+2,620	тюль	шина, 2500, в нише потолка, вынос 150	+2,620	2610, низ 10 (парит)	вручную
Т7	1, пом. 4	1320×1500, подок. 900	+2,620	портьеры	шина, 1820, в нише потолка, вынос 150	+2,620	2610, низ 10 (парит)	вручную
Т8	1, пом. 4	1320×1500, подок. 900	+2,620	тюль	шина, 1820, в нише потолка, вынос 150	+2,620	2610, низ 10 (парит)	вручную
Т13	1, пом. 6	1650×1500, подок. 900	+2,620	портьеры	шина, 2250, в нише потолка, вынос 150	+2,620	2610, низ 10 (парит)	вручную
Т14	1, пом. 6	1650×1500, подок. 900	+2,620	тюль	шина, 2250, в нише потолка, вынос 150	+2,620	2610, низ 10 (парит)	вручную
Т15	2, пом. 6	1320×1400, подок. 900	+2,620	римская штора	карниз, 1400, в нише потолка, вынос 60	+2,620	1620, низ 1000	шнур, петля низом 1500, натяжитель

Задания смежникам

Кому	Задание	Пом.
Гипсокартонщик	окно 1 (2100×1500, Т1, Т2): ниша под шторы 150×120, верх +2,620; закладная под шину L 2500 по всей длине — до обшивки	1
Гипсокартонщик	окно 1 (1320×1500, Т7, Т8): ниша под шторы 150×120, верх +2,620; закладная под шину L 1820 по всей длине — до обшивки	4
Гипсокартонщик	окно 1 (1650×1500, Т13, Т14): ниша под шторы 150×120, верх +2,620; закладная под шину L 2250 по всей длине — до обшивки	6
Гипсокартонщик	окно 2 (1320×1400, Т15): ниша под шторы 150×120, верх +2,620; закладная под шину L 1400 по всей длине — до обшивки	6
Электрик	выводы под электрокарнизы не требуются (управление вручную)	

Условные обозначения

- портьеры в открытом положении
- римская штора: сложена / опущена
- верх ниши под шторы в потолке
- тюль (на виде окна — прозрачная плашка)
- шина или карниз на отметке верха
- оконный проём

Допущения и предложения на листе

Основа листа: размеры сняты со скана плана заказчика по размерным цепочкам, контрольный обмер на объекте не выполнялся (К-13); высота потолка 2700 мм принята: на плане заказчика не указана (К-11); толщины стен приняты: наружные 250 мм, перегородки 150 мм (на плане 85–190 мм) (К-13); разрешённая мощность 15 кВт принята по типовой квартире, технических условий нет (К-14); утолщение стены 190 × 1360 мм и элемент 1470 × 160 мм плана заказчика не определены (К-12); ниши санузла 2 закрыты перегородкой и фальш-стеной: проектное решение, на плане заказчика ниша у входа открыта (К-18); несущие стены не определены: до технического заключения все существующие стены считаются несущими (К-20); окна существующие и сохраняются; подоконная доска и глубина откосов не заданы — приняты, не замерены (К-27); подрайон климата не задан — принят не северный (жилые от 2,5 м) (К-29).
Знак «**» — предложение проектировщика, заказчиком не утверждено (согласовать с заказчиком): К-25: дверь пом. 6 (стена В) — Было смещение 925: простенок до шахты Ш2 50 мм (в чистоте 26 мм по раскладке плитки) — короб скрытой двери и ряд плитки не помещаются.
См. лист открытых вопросов (лист 7, записи К-11–К-14, К-18, К-20; лист 8, записи К-25, К-27, К-29).

Примечания

1. Отметки — от чистого пола помещения; размеры — мм.
2. Шины в нишах потолка: закладная (брус или профиль) по всей длине ниши — до обшивки ГКЛ; ниша и её отметка — узел ниши на плане потолков (лист 59).
3. Шина в нише — на отметке верха ниши (крепление к закладной в потолке ниши); длина полотна — от верха шины до чистого пола за вычетом зазора.
4. Полотно портьер «парит» над полом на 10 мм; сборка портьер — 2,0, тюля — 2,5 (ширина полотна — в ведомости текстиля).
5. Шнур римской шторы — с натяжителем, петля низом не ниже 1500 мм от пола (защита детей; EN 13120 — рекомендация).
6. Электрокарнизы не предусмотрены; при замене на электропривод — вывод кабеля в нише у края шины (задание электрику).
7. Марки изделий — по плану текстиля и декора (лист 72) и ведомости текстиля (лист 74).

Изм.	Кол.уч	Лист	№ док.	Подп.	Дата
Разраб.		Кырлан А.С.			13.11.26
Пров.					
ГИП					
Н. контр.					
Утв.					

ГД-2026-003-АИ

Трёхкомнатная квартира

Общая площадь 78,95* м² · * размеры со скана, не замерены (реестр — л. 6–11, К-13)

Дизайн-проект интерьера трёхкомнатной квартиры

Стадия	Лист	Листов
РП	73	132

Шторы и карнизы

М б/м

Кырлан Александр Сергеевич

Ведомость текстиля

Шторы, тюль, римские шторы, ковры, подушки и пледы · размеры в мм · марки — по плану текстиля и декора

Текстиль: шторы, ковры, подушки, пледы

Поз.	Пом.	Изделие	Размер, мм	Ткань, состав, плотность	Сборка, ширина полотна		Цвет (система, код)	Кол.	Примечание
T1	1	Портьеры-волна	шина 2500 × полотно 2610	лён с блэкаут-подкладкой; лён 100 %; 320 г/м²	× 2, ширина 5000		Tikkurila H487 (Pumice)	2	низ 10 (парит); в нише потолка
T2	1	Тюль	шина 2500 × полотно 2610	вуаль; полиэстер 100 %	× 2,5, ширина 6250		Tikkurila V503 (Winter)	1	низ 10 (парит); в нише потолка
T3	1	Ковёр под кроватью	2800×1850	шерсть, ручное ткачество; шерсть 80 %, хлопок 20 %			NCS S 3005-Y20R (тёплый тауп-серый)	1	противоскользящая подложка; ворс 10 мм
T4	1	Подушки декоративные на кровать	500×500	лён 100 %			Tikkurila H487 (Pumice)	2	на C1
T5	1	Подушки на кровать, акцент	400×600	хлопковый бархат 100 %			Farrow & Ball No. 30 (Hague Blue)	2	на C1
T6	1	Плед на кровать	1300×1700	шерсть мериноса 100 %			Farrow & Ball No. 30 (Hague Blue)	1	на C1
T7	4	Портьеры-волна	шина 1820 × полотно 2610	лён с блэкаут-подкладкой; лён 100 %; 320 г/м²	× 2, ширина 3640		Tikkurila H487 (Pumice)	2	низ 10 (парит); в нише потолка
T8	4	Тюль	шина 1820 × полотно 2610	вуаль; полиэстер 100 %	× 2,5, ширина 4550		Tikkurila V503 (Winter)	1	низ 10 (парит); в нише потолка
T9	4	Ковёр под кроватью	2500×1800	шерсть, плоское плетение; шерсть 100 %			Tikkurila V484 (Driftwood)	1	противоскользящая подложка; ворс 8 мм
T10	4	Подушки декоративные на кровать	500×500	букле (шерсть 60 %, полиэстер 40 %)			Farrow & Ball No. 229 (Elephant's Breath)	2	на C7
T11	4	Подушки на кровать, акцент	400×600	хлопковый бархат 100 %			Farrow & Ball No. 47 (Green Smoke)	2	на C7
T12	4	Плед на кровать	1300×1700	шерсть мериноса 100 %			Farrow & Ball No. 30 (Hague Blue)	1	на C7
T13	6	Портьеры-волна (гостиная)	шина 2250 × полотно 2610	лён 70 %, вискоза 30 %; 280 г/м²	× 2, ширина 4500		Tikkurila H487 (Pumice)	2	низ 10 (парит); в нише потолка
T14	6	Тюль (гостиная)	шина 2250 × полотно 2610	вуаль; полиэстер 100 %	× 2,5, ширина 5625		Tikkurila V503 (Winter)	1	низ 10 (парит); в нише потолка
T15	6	Римская штора (кухня)	карниз 1400 × полотно 1620	лён 100 %			Tikkurila V484 (Driftwood)	1	низ 1000; в нише потолка; шнур: петля 1500, натяжитель
T16	6	Ковёр в зоне отдыха	3000×1150	шерсть, петля; шерсть 100 %			Tikkurila V484 (Driftwood)	1	противоскользящая подложка; ворс низкий
T17	6	Подушки на диван	500×500	букле (шерсть 60 %, полиэстер 40 %)			Tikkurila H487 (Pumice)	2	на M2
T18	6	Подушки на диван, акцент	400×600	хлопковый бархат 100 %			Farrow & Ball No. 30 (Hague Blue)	2	на M2
T19	6	Плед на диван	1300×1700	альпака 50 %, шерсть 50 %			Tikkurila V484 (Driftwood)	1	на M2
T20**	2	Полотенца банные махровые, дымчатый зелёный, сложены на полотенцесушителе	700×1400	махра; хлопок 100 %; 550 г/м²			Farrow & Ball No. 47 (Green Smoke)	2	на П10**; уход: 40 °C, без кондиционера
T21**	2	Полотенца для рук вафельные, белые, на нижних перекладинах сушителя	500×900	вафельное полотно; хлопок 100 %; 280 г/м²			Tikkurila V503 (Winter)	2	на П10**; уход: 60 °C
T22**	2	Коврик для ванной у бортика ванны, хлопок тафтинг, грейж	800×450	хлопок 100 %, латексная противоскользящая основа			Tikkurila H487 (Pumice)	1	противоскользящая подложка; ворс 12 мм; уход: 40 °C
T23**	7	Полотенца для рук вафельные, дымчатый зелёный, на полотенцесушителе	500×900	вафельное полотно; хлопок 100 %; 280 г/м²			Farrow & Ball No. 47 (Green Smoke)	2	на П13**; уход: 60 °C
T24**	7	Полотенце банное махровое, белое, сложено на сушителе	700×1400	махра; хлопок 100 %; 550 г/м²			Tikkurila V503 (Winter)	1	на П13**; уход: 40 °C, без кондиционера
T25**	5	Ковёр-дорожка шерстяной безворсовый 700×2000, серо-бежевый	700×2000	шерсть, плоское плетение; шерсть 100 %			Tikkurila V484 (Driftwood)	1	противоскользящая подложка; ворс 4 мм

образец цвета — по HEX производителя краски, справочно

Итого: шторы и тюль — 10 шт.; ковры и дорожки — 5 шт.; подушки, пледы, покрывала — 22 шт.

Примечания

1. Коды цвета — ориентир подбора по веерам производителей красок; ткань утверждается по образцу при дневном свете и при свете проекта 2700–3000 K.
2. Размеры полотен — по замеру после чистовой отделки пола и потолка; ширина полотна указана с учётом сборки, без припусков на швы. Схемы окон и отметки шин лист 73.
3. Портьеры и тюль — на тесьме «волна» по системе шины; блэкаут — подкладкой. Ковры — на противоскользящей подложке.
4. Замена изделия — аналогом по характеристикам (состав, плотность, размер, цвет по образцу) с согласованием автора проекта.
5. Места изделий — план текстиля и декора (лист 72); подушки и пледы — по марке мебели.

Допущения и предложения на листе. Знак «**» предложено (согласовать). См. лист открытых вопросов (листы 6–11).

Изм.	Кол.уч	Лист	№ док.	Подп.	Дата
Разраб.		Кырлан А.С.			13.11.26
Пров.					
ГИП					
Н. контр.					
Утв.					

ГД-2026-003-АИ

Трёхкомнатная квартира

Общая площадь 78,95* м² · * размеры со скана, не замерены (реестр — л. 6–11, К-13)

Дизайн-проект интерьера трёхкомнатной квартиры

Стадия	Лист	Листов
РП	74	132

Ведомость текстиля

М б/м

Кырлан Александр Сергеевич

выпуск 13.11.2026 № 6f3a8abb2c · стр. 82 из 157

Ведомость декора

Картины, зеркала, растения, настольный декор · высоты — мм от чистого пола

Декор: картины, зеркала, растения, предметы

Поз.	Пом.	Предмет	Размер, мм	Место: стена, высота от пола, мм	Масса, кг	Крепёж и основание	Свет места, отделка	Кол.
ДК1	1	Картина над кроватью: Серо-синяя абстракция, холст	1200×700	стена А, привязка 2250; низ 1300, центр 1650; над С1	4	подвес по основанию, 2 точки	рама — дуб	1
ДК2	2	Зеркало над умывальником, влагостойкое	600×750	стена Г, привязка 1150; низ 1100, центр 1475	4	подвес по основанию, 2 точки		1
ДК3	4	Картина над кроватью: Горизонт над полем, карандаш	1000×700	стена А, привязка 1545; низ 1300, центр 1650; над С7	4	подвес по основанию, 2 точки	рама — дуб	1
ДК4	4	Зеркало в рост в тонкой чёрной раме	600×1600	стена Г, привязка 700; низ 300, центр 1100	12	анкер для пустотелых оснований, 4 шт.; основание: перегородка — определить обмером до монтажа; нагрузка 30 кг	рама — чёрный матовый металл	1
ДК5	5	Зеркало	800×1800	стена Б, привязка 525; низ 550, центр 1450	18	анкер, 4 шт.; основание: перегородка — определить обмером до монтажа; нагрузка 40 кг	рама — чёрный матовый металл	1
ДК6	6	Картина: Песок и грейж с сине-зелёным акцентом	1200×900	стена Г, привязка 725; центр 1550	6	анкер, 2 шт.; основание: перегородка — определить обмером до монтажа; нагрузка 15 кг		1
ДК7	6	Растение	450×450	напольное			свет средний	1
ДК8	6	Ваза керамическая с ветками на обеденном столе	200×350	на М5 (обеденный стол)				1
ДК9	7	Зеркало над умывальником, влагостойкое	500×700	стена Б, привязка 780; низ 1100, центр 1450	4	подвес по основанию, 2 точки		1
ДК10**	2	Ваза-бутыль глазурованная, дымчатый зелёный, с сухой веткой эвкалипта — на полке короба инсталляции	130×450	напольное			Farrow & Ball No. 47 (Green Smoke)	1
ДК12**	7	Ваза-кувшин керамическая, тёплый серый, с сухоцветом (лагурус) — на полке короба инсталляции	130×400	напольное			Farrow & Ball No. 229 (Elephant's Breath)	1
ДК13**	5	Графика в тонкой чёрной раме 350×500: Силуэты сосен на склоне, тушь	350×500	стена Г, привязка 2105; низ 1250, центр 1500	2	дюбель с крюком, 2 точки; основание: перегородка — определить обмером до монтажа; нагрузка 10 кг	рама — чёрный матовый металл	1
ДК14**	8	Картина в коридоре: Пустой морской берег в пасмурный день, акварель	800×600	стена В, привязка 1875; низ 1200, центр 1500	3	дюбель с крюком, 2 точки; основание: перегородка — определить обмером до монтажа; нагрузка 10 кг	рама — дуб	1
ДК15**	1	Зеркало в рост в тонкой чёрной раме 600×1600	600×1600	стена В, привязка 3300; низ 300, центр 1100	12	анкер для пустотелых оснований, 4 шт.; основание: перегородка — определить обмером до монтажа; нагрузка 30 кг	рама — чёрный матовый металл	1
ДК16**	1	Сансевиерия в напольном керамическом кашпо Ø350, тёплый серый	400×400	напольное			свет слабый	1
ДК20**	4	Замиокулькас в напольном керамическом кашпо Ø350, тёплый серый	400×400	напольное			свет средний	1
ДК24**	6	Картина над креслом М4: Песчаные дюны на закате, пастель	1000×700	стена А, привязка 3525; низ 1250, центр 1600	4	дюбель с крюком, 2 точки; основание: перегородка — определить обмером до монтажа; нагрузка 10 кг	рама — дуб	1

Допущения и предложения на листе

Основа листа: размеры сняты со скана плана заказчика по размерным цепочкам, контрольный обмер на объекте не выполнялся (К-13); высота потолка 2700 мм принята: на плане заказчика не указана (К-11); толщины стен приняты: наружные 250 мм, перегородки 150 мм (на плане 85–190 мм) (К-13); разрешённая мощность 15 кВт принята по типовой квартире, технических условий нет (К-14); утолщение стены 190 × 1360 мм и элемент 1470 × 160 мм плана заказчика не определены (К-12); ниши санузла 2 закрыты перегородкой и фальш-стеной: проектное решение, на плане заказчика ниша у входа открыта (К-18); несущие стены не определены: до технического заключения все существующие стены считаются несущими (К-20); окна существующие и сохраняются; подоконная доска и глубина откосов не заданы — приняты, не замерены (К-27); подрайон климата не задан — принят не северный (жилые от 2,5 м) (К-29).

Знак «**» — предложение проектировщика, заказчиком не утверждено (согласовать с заказчиком): ИЗ-20: ДК15, ДК16, ДК10, ДК20, ДК13, ДК24, ДК12, ДК14.

Изменения по листу без подписи: ИЗ-20.

См. лист открытых вопросов (лист 7, записи К-11–К-14, К-18, К-20; лист 8, записи К-27, К-29; лист 11, запись ИЗ-20).

Примечания

1. Высоты — от чистого пола помещения до низа изделия, «ц» — до центра; привязки — от чистовой грани угла стены, мм.
2. Над мебелью низ изделия — на 150–250 мм выше спинки или изголовья; без мебели центр — на 1450–1600 мм от пола.
3. Изделия до 5 кг — на два подвеса по основанию; тяжелее — на анкеры с нагрузкой не меньше двойной массы; на ГКЛ — только по закладной или анкеру для пустотелых оснований.
4. Зеркала в рост — с креплением от опрокидывания; в санузлах — влагостойкие, на клей для зеркал и нейтральный силикон.
5. Места изделий — план текстиля и декора (лист 72). Схемы развески — лист 76.

Изм.	Кол.уч	Лист	№ док.	Подп.	Дата
Разраб.		Кырлан А.С.			13.11.26
Пров.					
ГИП					
Н. контр.					
Утв.					

ГД-2026-003-АИ

Трёхкомнатная квартира

Общая площадь 78,95* м² · * размеры со скана, не замерены (реестр — л. 6–11, К-13)

Дизайн-проект интерьера трёхкомнатной квартиры

Стадия	Лист	Листов
РП	75	132

Ведомость декора

М б/м

Кырлан Александр Сергеевич


Схемы развески

Схемы развески картин и зеркал (М 1:50) · высоты — мм от чистого пола


Ведомость декора (размер, масса, крепёж и основание) — лист 75

картина · зеркало · мебель под изделием


ДК1 — Спальня 1 (пом. 1), стена А (М 1:50)

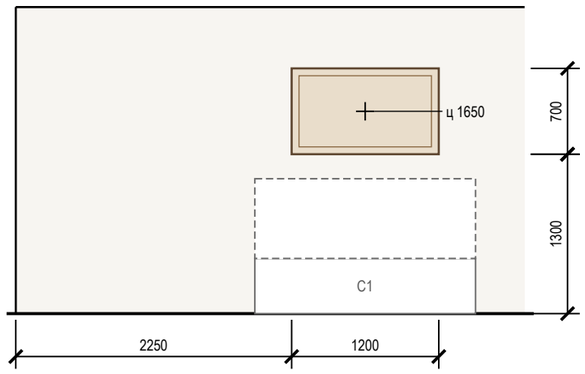


ДК2 — Ванная (пом. 2), стена Г (М 1:50)

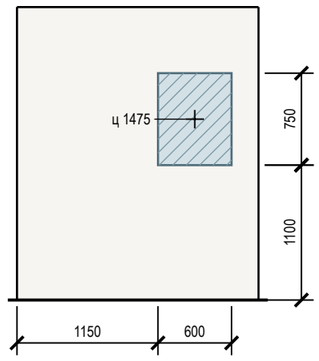


ДК3 — Спальня 2 (пом. 4), стена А (М 1:50)

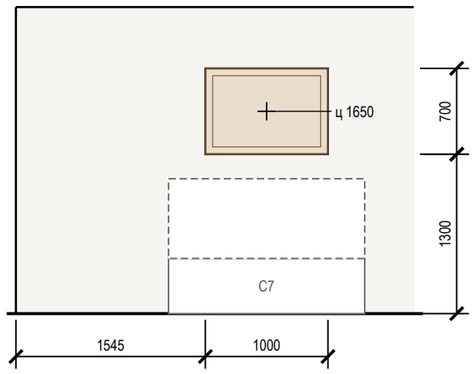


ДК4 — Спальня 2 (пом. 4), стена Г (М 1:50)

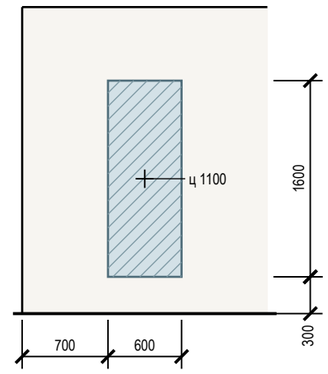


ДК9 — Санузел 2 (пом. 7), стена Б (М 1:50)

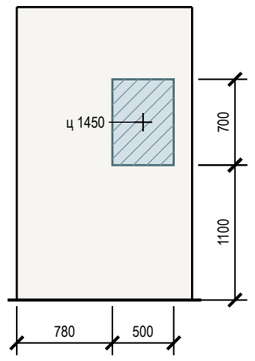


ДК5 — Прихожая (пом. 5), стена Б (М 1:50)

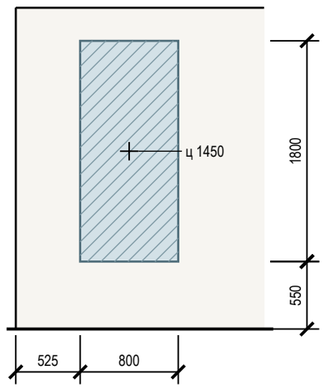


ДК6 — Кухня-гостиная (пом. 6), стена Г (М 1:50)

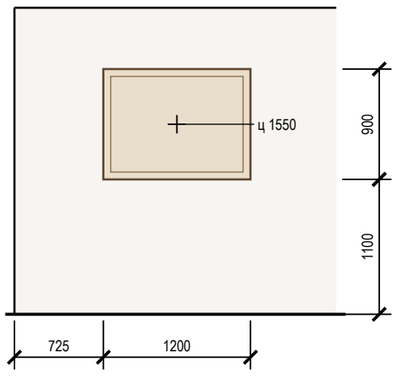


ДК13 — Прихожая (пом. 5), стена Г (М 1:50)**

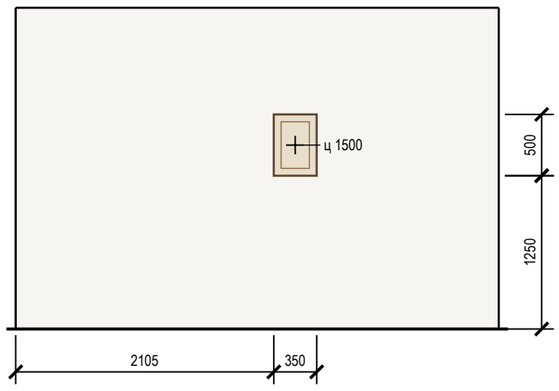


ДК14 — Коридор (пом. 8), стена В (М 1:50)**

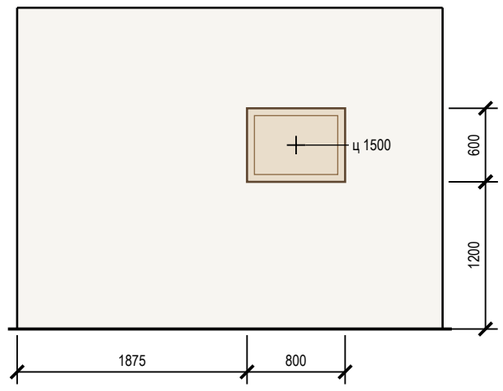

ДК15 — Спальня 1 (пом. 1), стена В (М 1:50)**

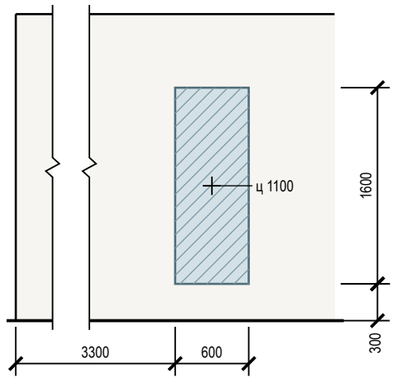

ДК24 — Кухня-гостиная (пом. 6), стена А (М 1:50)**

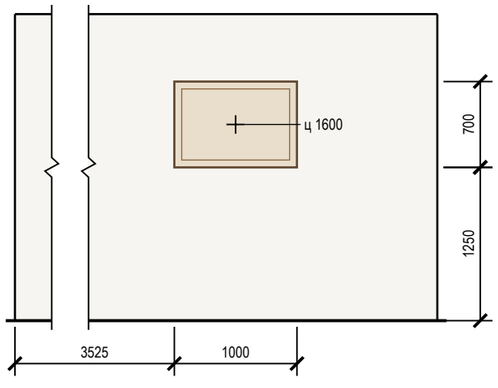

Допущения и предложения на листе

Основа листа: размеры сняты со скана плана заказчика по размерным цепочкам, контрольный обмер на объекте не выполнялся (К-13); высота потолка 2700 мм принята: на плане заказчика не указана (К-11); толщины стен приняты: наружные 250 мм, перегородки 150 мм (на плане 85–190 мм) (К-13); разрешённая мощность 15 кВт принята по типовой квартире, технических условий нет (К-14); утолщение стены 190 × 1360 мм и элемент 1470 × 160 мм плана заказчика не определены (К-12); ниши санузла 2 закрыты перегородкой и фальш-стеной: проектное решение, на плане заказчика ниша у входа открыта (К-18); несущие стены не определены: до технического заключения все существующие стены считаются несущими (К-20); окна существующие и сохраняются; подоконная доска и глубина откосов не заданы — приняты, не замерены (К-27); подрайон климата не задан — принят не северный (жилые от 2,5 м) (К-29).

Знак «**» — предложение проектировщика, заказчиком не утверждено (согласовать с заказчиком): ИЗ-20: ДК15, ДК13, ДК24, ДК14.

См. лист открытых вопросов (лист 7, записи К-11–К-14, К-18, К-20; лист 8, записи К-27, К-29; лист 11, запись ИЗ-20).

Примечания

1. Высоты — от чистого пола помещения до низа изделия, «ц» — до центра; привязки — от чистовой грани угла стены, мм.
2. Над мебелью низ изделия — на 150–250 мм выше спинки или изголовья; без мебели центр — на 1450–1600 мм от пола.
3. Изделия до 5 кг — на два подвеса по основанию; тяжелее — на анкеры с нагрузкой не меньше двойной массы; на ГКЛ — только по закладной или анкеру для пустотелых оснований.
4. Зеркала в рост — с креплением от опрокидывания; в санузлах — влагостойкие, на клей для зеркал и нейтральный силикон.
5. Места изделий — план текстиля и декора (лист 72). Ведомость декора: размер, масса, крепёж и основание — лист 75.

Изм.	Кол.уч	Лист	№ док.	Подп.	Дата
Разраб.		Кырлан А.С.			13.11.26
Пров.					
ГИП					
Н. контр.					
Утв.					

ГД-2026-003-АИ

Трёхкомнатная квартира

Общая площадь 78,95* м² · * размеры со скана, не замерены (реестр — л. 6–11, К-13)

Дизайн-проект интерьера трёхкомнатной квартиры

Стадия	Лист	Листов
РП	76	132

Схемы развески

М б/м


Кырлан Александр Сергеевич

выпуск 13.11.2026 № 6f3a8abb2c · стр. 84 из 157

Встроенная мебель. Схема расположения

встроенная и корпусная мебель на заказ, кухонный гарнитур · размеры в мм · марки — по ведомости изделий

ПРЕДВАРИТЕЛЬНО · не для производства работ · открыто пунктов: 28 (реестр — л. 6–11)

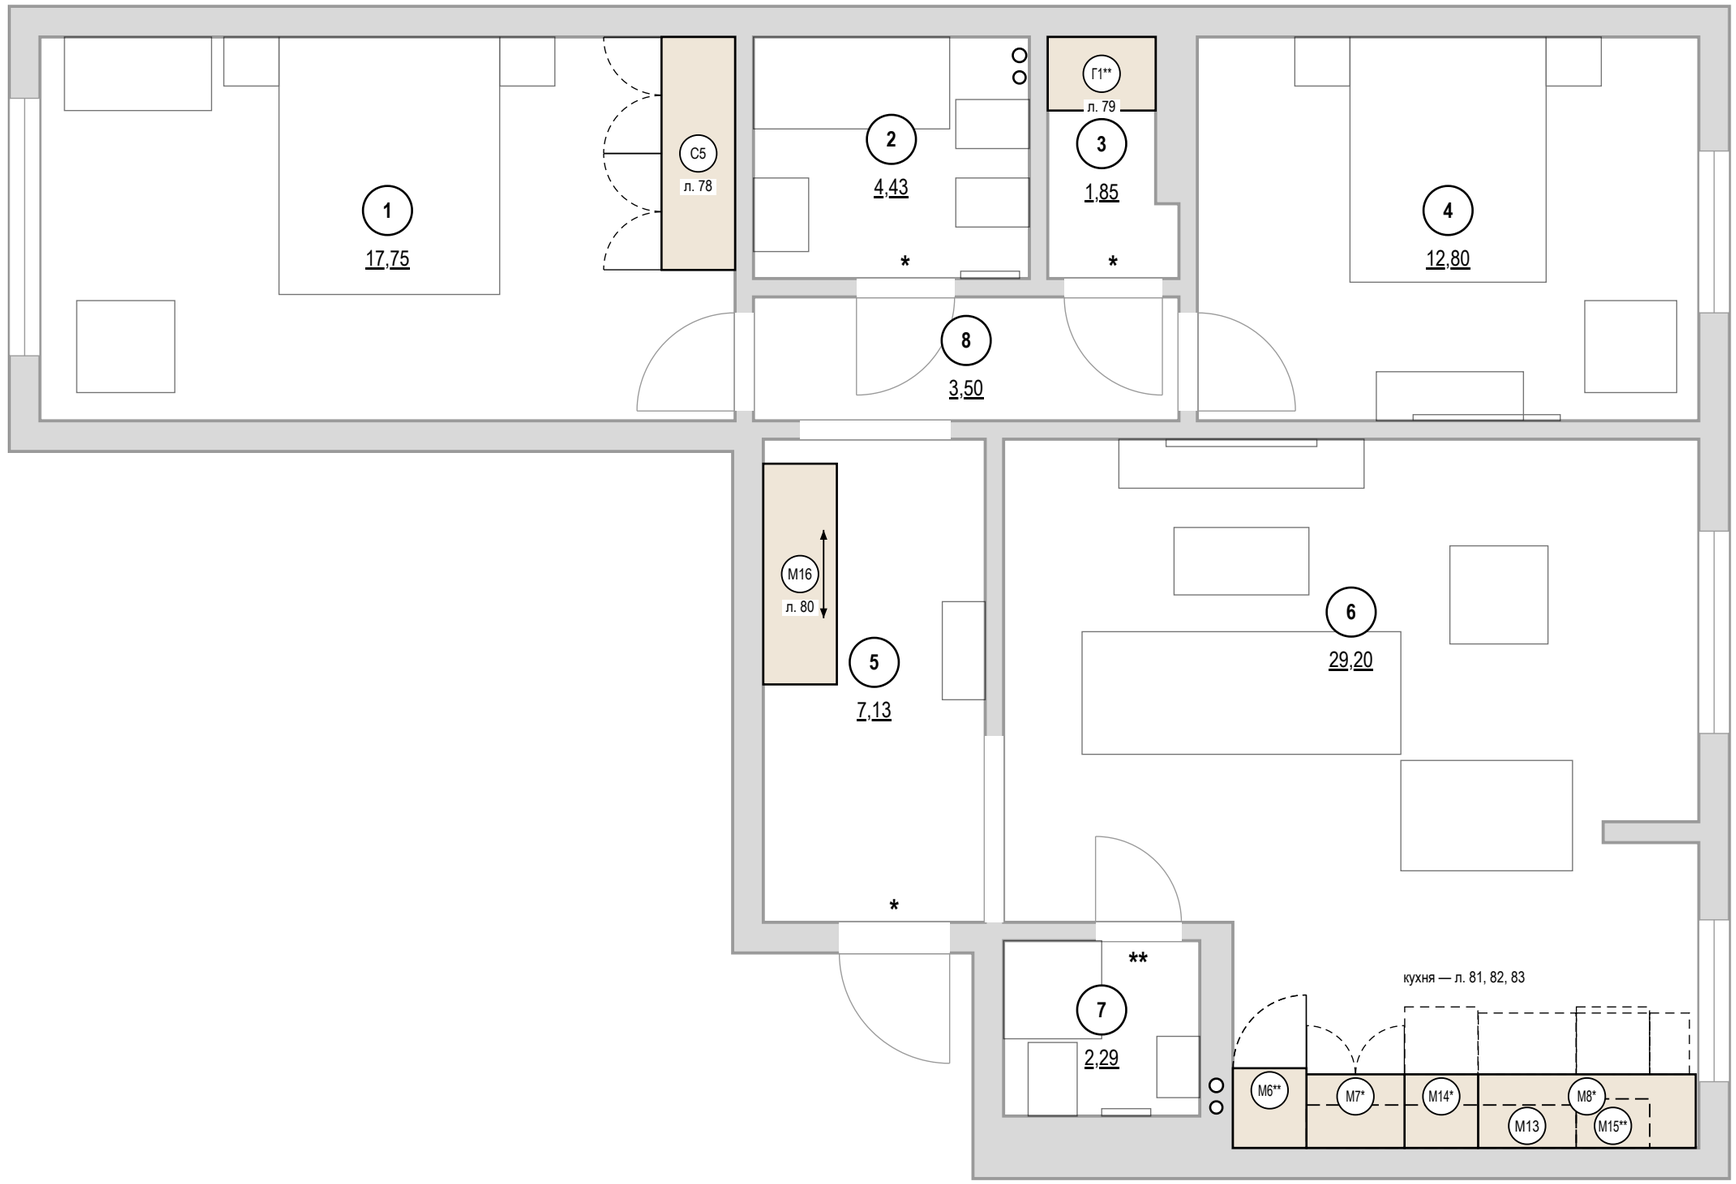

Ведомость изделий

Марка	Наименование	Пом.	Ш×Г×В, мм	Лист
C5	Шкаф распашной	1	1900×600×2400	78
Г1**	Система хранения	3	880×600×2400	79
M16	Шкаф-купе	5	1800×600×2600	80
M8*	Модуль нижний: карго, духовой шкаф, ящики, варочная	6	1775×600×900	81, 82
M15**	Модуль навесной: полки	6	600×400×570	81, 82
M13	Модуль навесной: полки, сушка	6	2200×350×720	81, 82
M14*	Модуль под ПММ 60: без корпуса, фасад на дверь машины	6	600×600×900	81, 82
M7*	Модуль нижний: мойка	6	800×600×900	81, 82
M6**	Пенал: холодильник встр.	6	600×650×2100	81, 82

Условные обозначения

- изделие мебельщика: корпус на полу
- невидимый контур: навесной модуль, корпус под столешницей
- открывание распашного фасада
- зона выдвижения ящика, двери техники
- дверь купе, стрелка — направление движения
- (K1) марка изделия или модуля (на схеме расположения под ней — лист изделия)
- * «*» — принято, не замерено и не подтверждено
- ** «**» — предложение проектировщика, заказчиком не утверждено

Примечания

1. Изделия — по чистовым размерам помещений; перед раскроем — контрольный замер цеха после чистовой отделки стен, пола и потолка.
2. Открывание фасадов и выдвижение ящиков показано в открытом положении: зоны не пересекают двери, радиаторы, выключатели и проходы.
3. Стояки и счётчики за мебелью — с сервисным люком; газовые трубы мебелью не зашиваются.
4. Покупная мебель — по плану расстановки мебели и спецификации дизайнера; здесь — подложкой.
5. Допущение проекта: кухня: раскладка гарнитура принята проектной, решение автора (ИЗ-12) — мойка M7* у шахты Ш2, ПММ M14* рядом с мойкой, варочная и духовой шкаф в M8*, вытяжка M15**, холодильник M6**; выводы техники — по типовой расстановке; условие: до начала черновых работ сверить раскладку и выводы с чертежом кухни от изготовителя, выводы пересматриваются по его чертежу (вопрос К-8).
6. Марки из допущений, которых нет на этом листе: Ш2 — лист 48.
7. Знак «*» у проёма — положение не замерено; реестр: листы 6–11, вопросы К-26, К-25.

1000 мм · печать 1:1

Допущения и предложения на листе. Знак «*» принято (замерить): Ст К1-1, Ст В1-1, Ст К1-2, Ст В1-2. Знак «**» предложено (согласовать). См. лист открытых вопросов (листы 6–11).

Изм.	Кол.уч	Лист	№ док.	Подп.	Дата
Разраб.		Кырлан А.С.			13.11.26
Пров.					
ГИП					
Н. контр.					
Утв.					

ГД-2026-003-АИ

Трёхкомнатная квартира

Общая площадь 78,95* м² · * размеры со скана, не замерены (реестр — л. 6–11, К-13)

Дизайн-проект интерьера трёхкомнатной квартиры

Стадия	Лист	Листов
РП	77	132

Встроенная мебель. Схема расположения

М 1:50

Кырлан Александр Сергеевич


выпуск 13.11.2026 № 6f3a8abb2c · стр. 85 из 157

Шкаф распашной С5


Спальня 1 (пом. 1) · вид из помещения · размеры в мм, отметки в м

ПРЕДВАРИТЕЛЬНО · не для производства работ · открыто пунктов: 28 (реестр — л. 6–11)


Вид с фасадами (М 1:20)

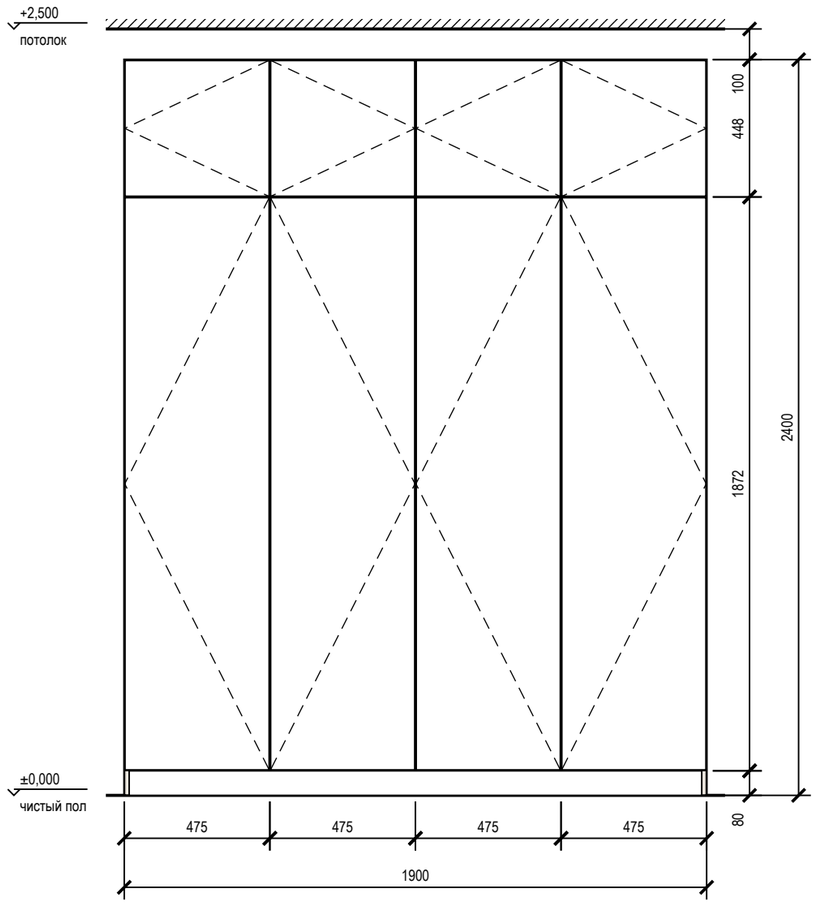


Вид без фасадов (М 1:20)

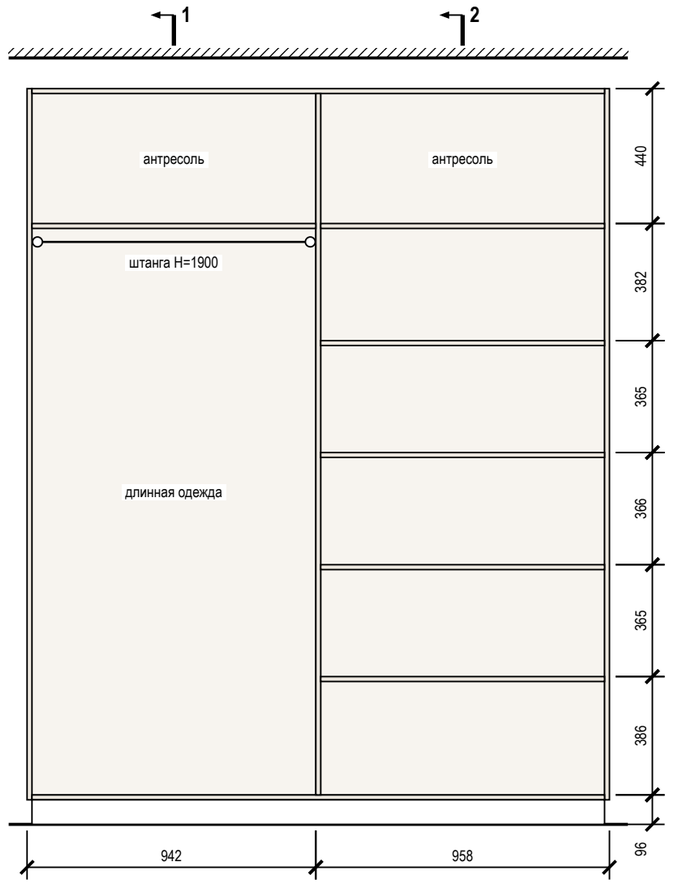

Разрез 1-1 (М 1:20)

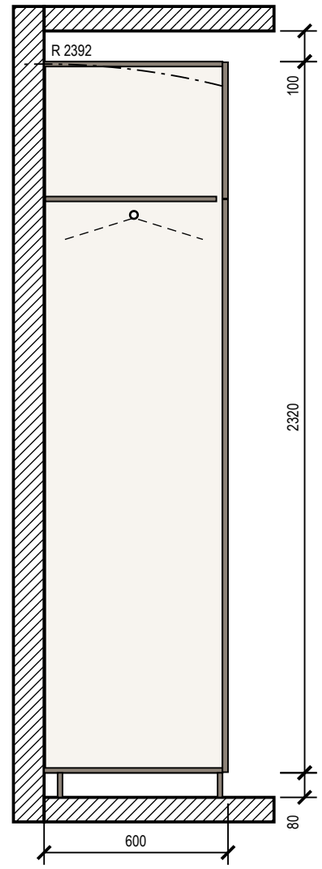

Разрез 2-2 (М 1:20)

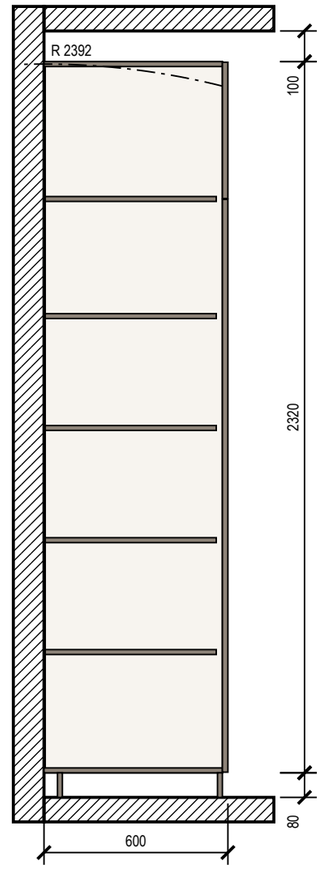

Примечания

1. Размеры — в мм по чистовой отделке; изделие 1900×600×2400 (Ш×Г×В). Перед раскроем — контрольный замер цеха после чистовой отделки стен, пола и потолка.
2. Корпус — ЛДСП 16 мм, задняя стенка ХДФ 4 мм в паз, цоколь 80 мм на регулируемых опорах; фасады накладные — МДФ 18 мм, эмаль матовая, 18 мм; цвет — по колерной карте; петли с доводчиком: фасад 1869 мм — 4 петли, фасад 445 мм — 2 петли.
3. Кромка: скрытые торцы 0,4 мм, видимые 2 мм (ПВХ/АБС).
4. Номинальные зазоры: между фасадами 3 мм, фасад — стена и фасад — потолок не менее 3 мм, фасад ящика — стойка 2 мм.
5. Присадка по 32-й системе — выполняет цех.
6. Зазор до потолка 100 мм — закрыть планкой в цвет корпуса при монтаже.
7. Подъём корпуса: диагональ боковины без цоколя √(2320² + 582²) = 2392 мм < 2500 мм до потолка — корпус собирается лёжа, поднимается поворотом и ставится на цоколь.
8. Крепление к стене от опрокидывания: уголок к стене, 2 шт.; основание стены и шаг анкеров — монтажная схема шкафов.

Условные обозначения

- фасад распашной: линии сходятся к стороне петель
- корпус и полки ЛДСП (вид на стену)
- задняя стенка ХДФ
- деталь в разрезе
- штанга для плечиков (на разрезе — плечики 450 мм)
- траектория угла корпуса при подъёме в проектное положение

Допущения и предложения на листе

Основа листа: размеры сняты со скана плана заказчика по размерным цепочкам, контрольный обмер на объекте не выполнялся (К-13); высота потолка 2700 мм принята: на плане заказчика не указана (К-11); толщины стен приняты: наружные 250 мм, перегородки 150 мм (на плане 85–190 мм) (К-13); разрешённая мощность 15 кВт принята по типовой квартире, технических условий нет (К-14); утолщение стены 190 × 1360 мм и элемент 1470 × 160 мм плана заказчика не определены (К-12); ниши санузла 2 закрыты перегородкой и фальш-стеной: проектное решение, на плане заказчика ниша у входа открыта (К-18); несущие стены не определены: до технического заключения все существующие стены считаются несущими (К-20); окна существующие и сохраняются; подоконная доска и глубина откосов не заданы — приняты, не замерены (К-27); подрайон климата не задан — принят не северный (жилые от 2,5 м) (К-29).

См. лист открытых вопросов (лист 7, записи К-11–К-14, К-18, К-20; лист 8, записи К-27, К-29).

1000 мм · печать 1:1

Изм.	Кол.уч	Лист	№ док.	Подп.	Дата
Разраб.		Кырлан А.С.			13.11.26
Пров.					
ГИП					
Н. контр.					
Утв.					

ГД-2026-003-АИ

Трёхкомнатная квартира

Общая площадь 78,95* м² · * размеры со скана, не замерены (реестр — л. 6–11, К-13)

Дизайн-проект интерьера трёхкомнатной квартиры

Стадия	Лист	Листов
РП	78	132

Шкаф распашной С5

М 1:20

Кырлан Александр Сергеевич


выпуск 13.11.2026 № 6f3a8abb2c · стр. 86 из 157

Система хранения Г1


Гардеробная (пом. 3) · вид из помещения · размеры в мм, отметки в м

ПРЕДВАРИТЕЛЬНО · не для производства работ · открыто пунктов: 28 (реестр — л. 6–11)


Общий вид (М 1:20)

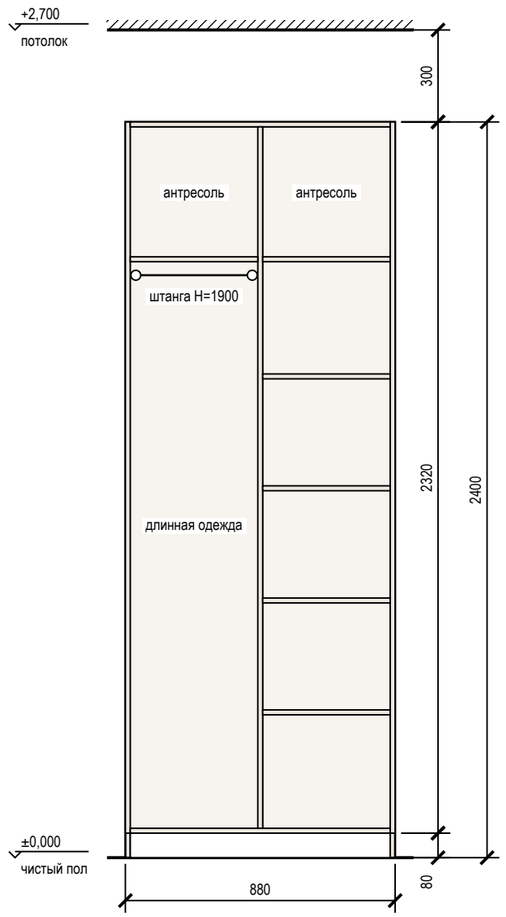


Наполнение, размеры в свету (М 1:20)

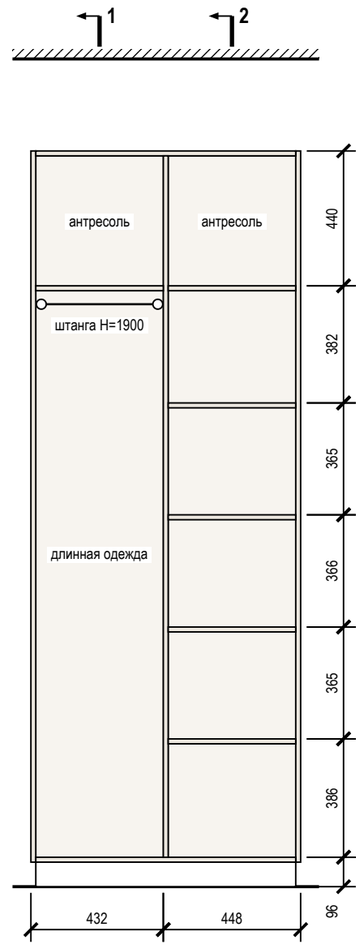

Разрез 1-1 (М 1:20)

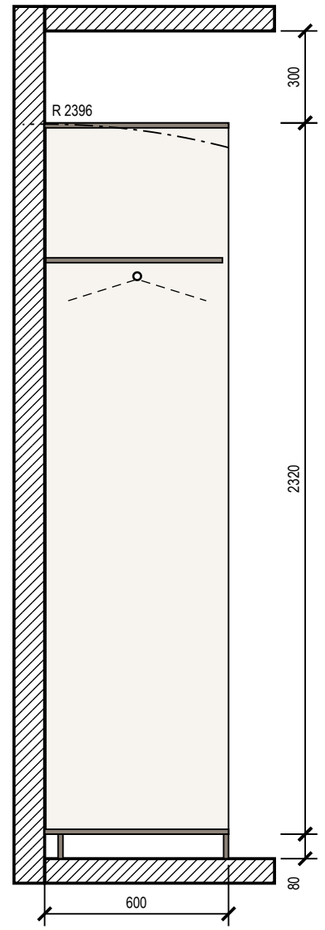

Разрез 2-2 (М 1:20)

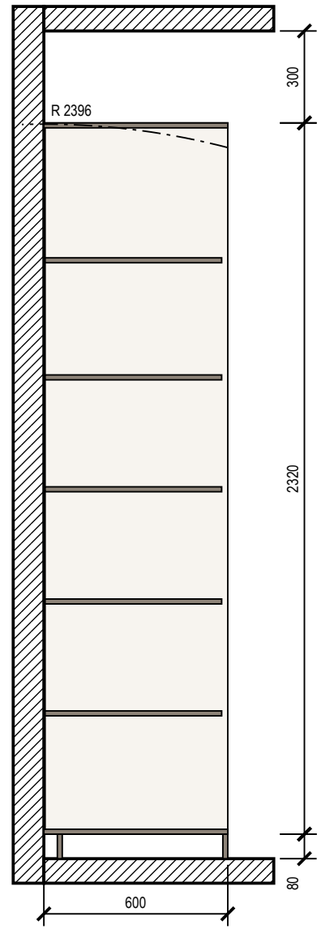

Примечания

1. Размеры — в мм по чистовой отделке; изделие 880×600×2400 (Ш×Г×В). Перед раскроем — контрольный замер цеха после чистовой отделки стен, пола и потолка.
2. Корпус — ЛДСП 16 мм, задняя стенка ХДФ 4 мм в паз, цоколь 80 мм на регулируемых опорах; открытая система: без фасадов.
3. Кромка: скрытые торцы 0,4 мм, видимые 2 мм (ПВХ/АБС).
4. Присадка по 32-й системе — выполняет цех.
5. Зазор до потолка 300 мм.
6. Подъём корпуса: диагональ боковины без цоколя √(2320² + 600²) = 2396 мм < 2700 мм до потолка — корпус собирается лёжа, поднимается поворотом и ставится на цоколь.
7. Крепление к стене от опрокидывания: крепление к стене, 3 точки; основание стены и шаг анкеров — монтажная схема шкафов.

Условные обозначения

- корпус и полки ЛДСП (вид на стену)
- задняя стенка ХДФ
- деталь в разрезе
- штанга для плечиков (на разрезе — плечики 450 мм)
- траектория угла корпуса при подъёме в проектное положение

Допущения и предложения на листе

Основа листа: размеры сняты со скана плана заказчика по размерным цепочкам, контрольный обмер на объекте не выполнялся (К-13); высота потолка 2700 мм принята: на плане заказчика не указана (К-11); толщины стен приняты: наружные 250 мм, перегородки 150 мм (на плане 85–190 мм) (К-13); разрешённая мощность 15 кВт принята по типовой квартире, технических условий нет (К-14); утолщение стены 190 × 1360 мм и элемент 1470 × 160 мм плана заказчика не определены (К-12); ниши санузла 2 закрыты перегородкой и фальш-стеной: проектное решение, на плане заказчика ниша у входа открыта (К-18); несущие стены не определены: до технического заключения все существующие стены считаются несущими (К-20); окна существующие и сохраняются; подоконная доска и глубина откосов не заданы — приняты, не замерены (К-27); подрайон климата не задан — принят не северный (жилые от 2,5 м) (К-29).

Открытые вопросы и конфликты по листу: К-9.

См. лист открытых вопросов (лист 6, запись К-9; лист 7, записи К-11–К-14, К-18, К-20; лист 8, записи К-27, К-29).

1000 мм · печать 1:1

Изм.	Кол.уч	Лист	№ док.	Подп.	Дата
Разраб.		Кырлан А.С.			13.11.26
Пров.					
ГИП					
Н. контр.					
Утв.					

ГД-2026-003-АИ

Трёхкомнатная квартира

Общая площадь 78,95* м² · * размеры со скана, не замерены (реестр — л. 6–11, К-13)

Дизайн-проект интерьера трёхкомнатной квартиры

Стадия	Лист	Листов
РП	79	132

Система хранения Г1

М 1:20


Кырлан Александр Сергеевич

выпуск 13.11.2026 № 6f3a8abb2c · стр. 87 из 157


Шкаф-купе М16

Прихожая (пом. 5) · вид из помещения · размеры в мм, отметки в м


Вид с фасадами (М 1:20)

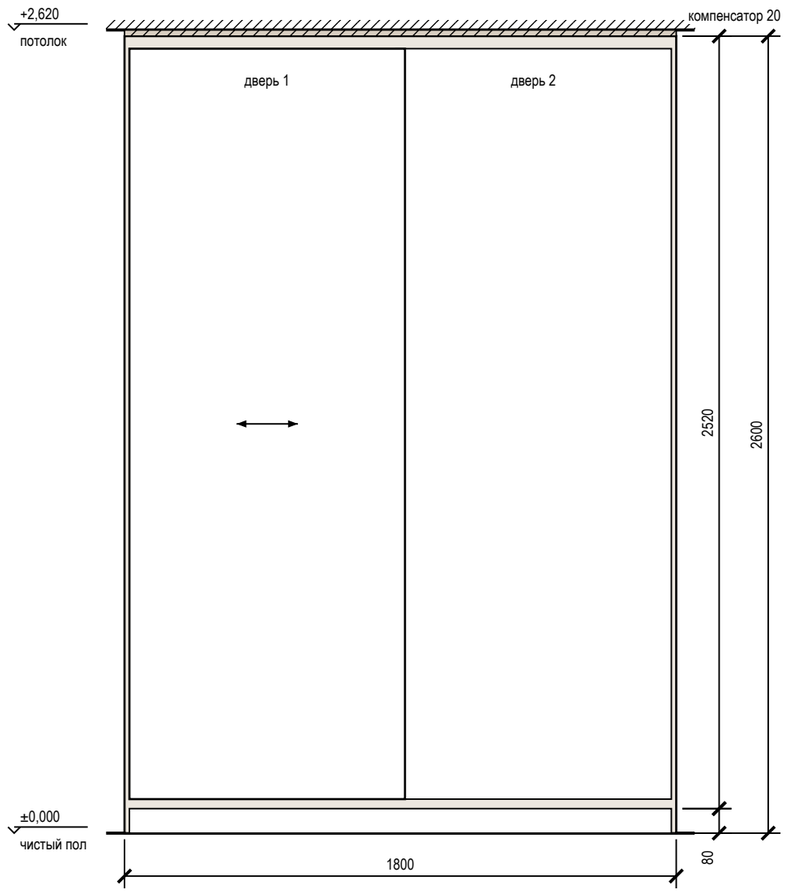


Вид без фасадов (М 1:20)

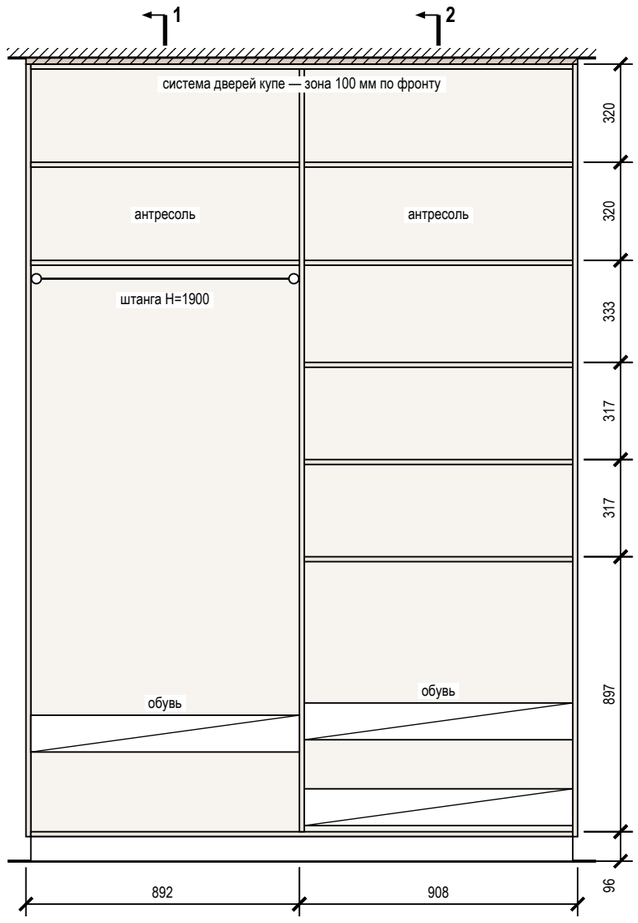

Разрез 1-1 (М 1:20)

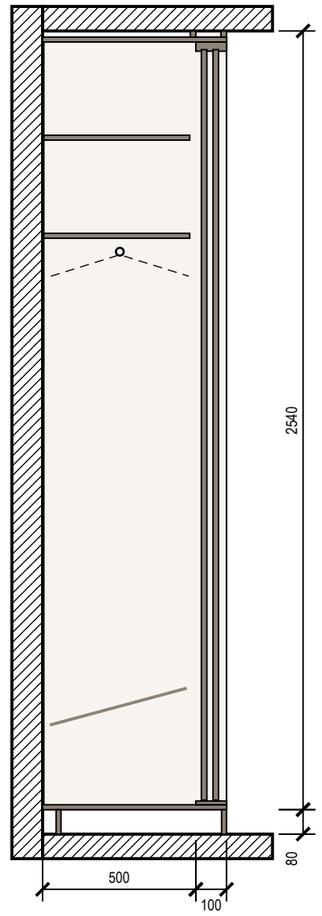

Разрез 2-2 (М 1:20)

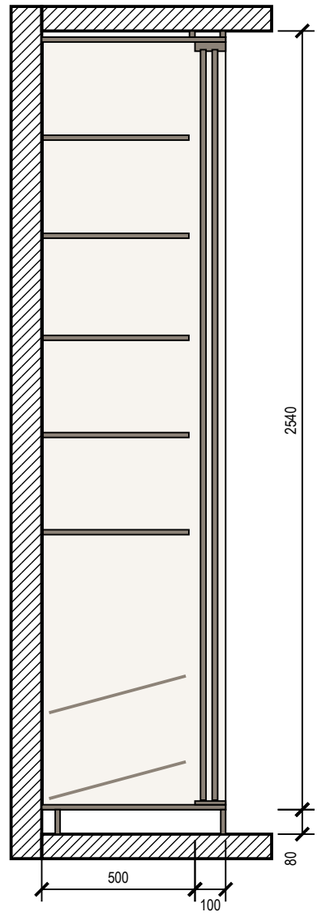

Примечания

1. Размеры — в мм по чистовой отделке; изделие 1800×600×2600 (Ш×Г×В). Перед раскроем — контрольный замер цеха после чистовой отделки стен, пола и потолка.
2. Корпус — ЛДСП 16 мм, задняя стенка ХДФ 4 мм в паз, цоколь 80 мм на регулируемых опорах; двери купе — ЛДСП 10 мм в алюминиевом профиле; нахлёст 30 мм, ширина двери 899 мм, высота — проём минус 40 мм; цвет — по колерной карте.
3. Кромка: скрытые торцы 0,4 мм, видимые 2 мм (ПВХ/АБС).
4. Номинальные зазоры: дверь купе — боковина 3 мм, фасад ящика — стойка 2 мм; ящики внутри купе — с накладкой 30 мм на стойке со стороны нахлёста дверей.
5. Присадка по 32-й системе — выполняет цех.
6. Компенсатор 20 мм — короб из ЛДСП по фронту и торцам, подгоняется к потолку при монтаже (припуск 20 мм), крепится к корпусу и к потолку.
7. Сборка стоя на месте (решение по изделию): корпус не собирается лёжа и не поднимается собранным — собирается в проектном положении у стены; траектория подъёма на виде не показана. Диагональ боковины без цоколя √(2520² + 600²) = 2590 мм < 2620 мм до потолка.
8. Крепление к стене от опрокидывания — уголки 2 шт. к несущему основанию (монтажная схема шкафов).

Условные обозначения

- дверь купе, стрелка — направление движения
- корпус и полки ЛДСП (вид на стену)
- задняя стенка ХДФ
- деталь в разрезе
- компенсатор — короб до потолка
- штанга для плечиков (на разрезе — плечики 450 мм)

Допущения и предложения на листе

Основа листа: размеры сняты со скана плана заказчика по размерным цепочкам, контрольный обмер на объекте не выполнялся (К-13); высота потолка 2700 мм принята: на плане заказчика не указана (К-11); толщины стен приняты: наружные 250 мм, перегородки 150 мм (на плане 85–190 мм) (К-13); разрешённая мощность 15 кВт принята по типовой квартире, технических условий нет (К-14); утолщение стены 190 × 1360 мм и элемент 1470 × 160 мм плана заказчика не определены (К-12); ниши санузла 2 закрыты перегородкой и фальш-стеной: проектное решение, на плане заказчика ниша у входа открыта (К-18); несущие стены не определены: до технического заключения все существующие стены считаются несущими (К-20); окна существующие и сохраняются; подоконная доска и глубина откосов не заданы — приняты, не замерены (К-27); подрайон климата не задан — принят не северный (жилые от 2,5 м) (К-29).
См. лист открытых вопросов (лист 7, записи К-11–К-14, К-18, К-20; лист 8, записи К-27, К-29).

1000 мм · печать 1:1

Изм.	Кол.уч	Лист	№ док.	Подп.	Дата
Разраб.		Кырлан А.С.			13.11.26
Пров.					
ГИП					
Н. контр.					
Утв.					

ГД-2026-003-АИ

Трёхкомнатная квартира

Общая площадь 78,95* м² · * размеры со скана, не замерены (реестр — л. 6–11, К-13)

Дизайн-проект интерьера трёхкомнатной квартиры

Стадия	Лист	Листов
РП	80	132

Шкаф-купе М16

М 1:20


Кырлан Александр Сергеевич

выпуск 13.11.2026 № 6f3a8abb2c · стр. 88 из 157

Кухня (пом. 6). Развёртка гарнитура

Кухня-гостиная (пом. 6) · стена В · вид из помещения · размеры в мм, отметки в м · лист 1: вид с фасадами

Вид с фасадами (М 1:20)

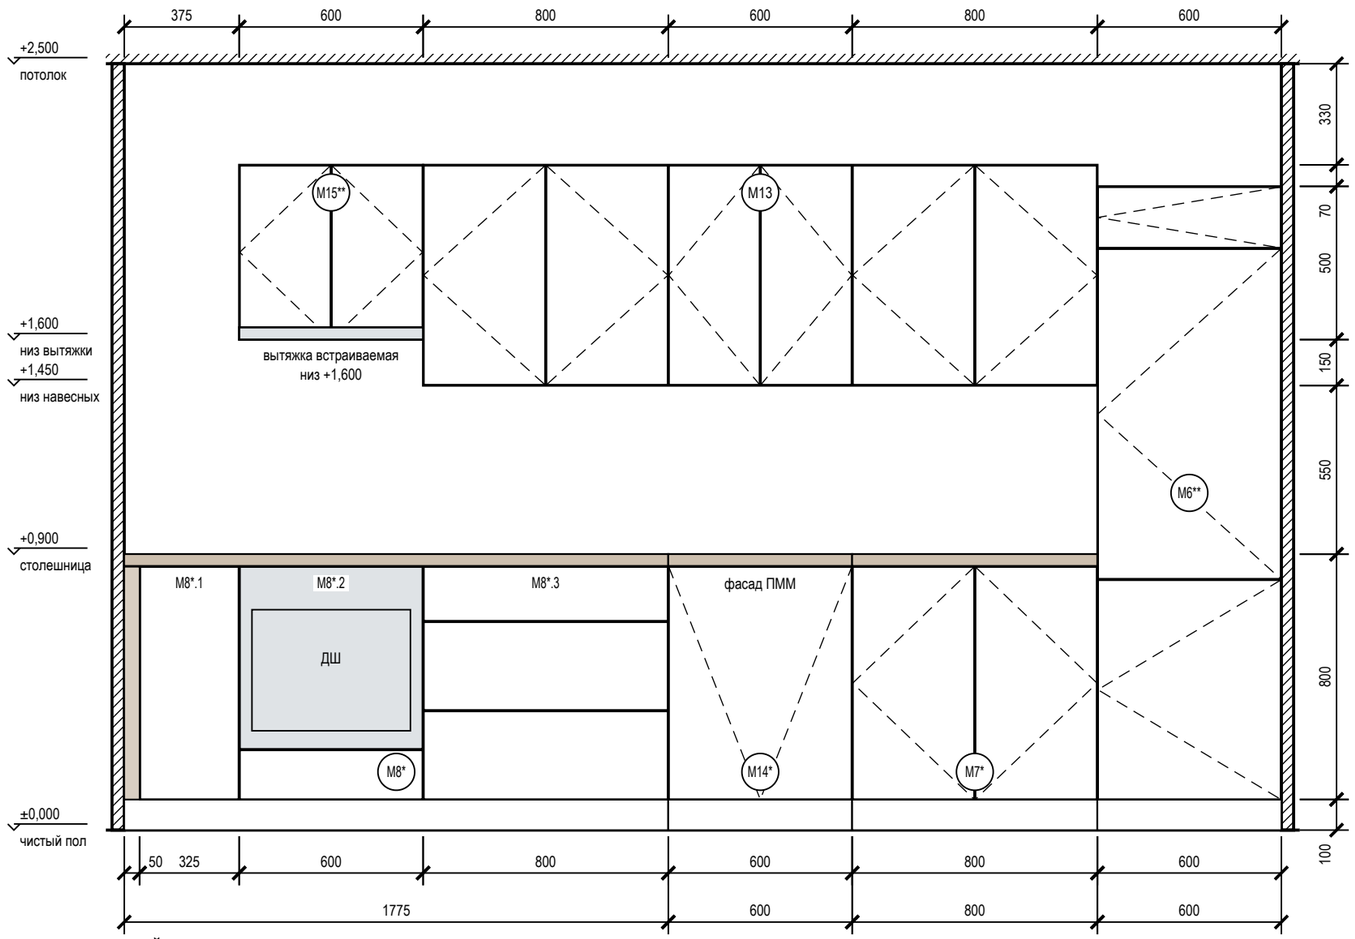

Условные обозначения

- фасад распашной: линии сходятся к стороне петель
- фасад ящика, карго
- встраиваемая техника
- столешница
- доборная планка
- деталь в разрезе
- К1 — марка изделия или модуля (на схеме расположения под ней — лист изделия)
- розетка на стене
- вывод кабеля к технике
- В1 — вывод воды В1 / Т3, канализации К1

Примечания

1. Размеры — в мм по чистовой отделке, вид из помещения; марки — как на плане расстановки. Перед раскроем контрольный замер цеха после фартука и пола.
2. Корпуса — ЛДСП 16 мм, задняя стенка ХДФ 4 мм; фасады — МДФ, эмаль матовая 18 мм, цвет по колерной карте; столешница 38 мм, свес 20 мм; цоколь 100 мм.
3. Кромка: скрытые торцы 0,4 мм, видимые 2 мм. Номинальные зазоры: между фасадами 3 мм, фасад — столешница 3 мм, фасад — стена не менее 3 мм.
4. Ящики полного выдвижения и петли — с доводчиком; присадка по 32-й системе — выполняет цех.

Ведомость модулей

Мод.	Наименование	Ш×Г×В, мм	Низ, мм
M8*	Модуль нижний: карго, духовой шкаф, ящики, варочная	1775×600×900	от цоколя
M14*	Модуль под ПММ 60: без корпуса, фасад на дверь машины	600×600×900	от цоколя
M7*	Модуль нижний: мойка	800×600×900	от цоколя

Мод.	Наименование	Ш×Г×В, мм	Низ, мм
M15**	Модуль навесной: полки	600×400×570	+1600
M13	Модуль навесной: полки, сушка	2200×350×720	+1450
M6**	Пенал: холодильник встр.	600×650×2100	от пола

Допущения и предложения на листе

Основа листа: размеры сняты со скана плана заказчика по размерным цепочкам, контрольный обмер на объекте не выполнялся (К-13); высота потолка 2700 мм принята: на плане заказчика не указана (К-11); толщины стен приняты: наружные 250 мм, перегородки 150 мм (на плане 85–190 мм) (К-13); разрешённая мощность 15 кВт принята по типовой квартире, технических условий нет (К-14); утолщение стены 190 × 1360 мм и элемент 1470 × 160 мм плана заказчика не определены (К-12); ниши санузла 2 закрыты перегородкой и фальш-стеной: проектное решение, на плане заказчика ниша у входа открыта (К-18); несущие стены не определены: до технического заключения все существующие стены считаются несущими (К-20); окна существующие и сохраняются; подоконная доска и глубина откосов не заданы — приняты, не замерены (К-27); подрайон климата не задан — принят не северный (жилые от 2,5 м) (К-29).

Знак «*» — принято, не замерено и не подтверждено (замерить на объекте): К-8: M7, M14; M8 — Ряд M6…M8 стена-в-стену: было 600+800+600+1800 = 3800 от х 9730 до черновой грани стены Б (13530); чистовая длина стены по развёртке 3770 (отделка 15/15) — гарнитур длиннее стены на 30 мм, зазора под компенсатор нет.

Знак «**» — предложение проектировщика, заказчиком не утверждено (согласовать с заказчиком): ИЗ-5, К-8: M6, M15.

Открытые вопросы и конфликты по листу: К-8, К-24.

См. лист открытых вопросов (лист 6, запись К-8; лист 7, записи К-11–К-14, К-18, К-20; лист 8, записи К-24, К-27, К-29; лист 9, запись ИЗ-5).

1000 мм · печать 1:1

Изм.	Кол.уч	Лист	№ док.	Подп.	Дата
Разраб.		Кырлан А.С.			13.11.26
Пров.					
ГИП					
Н. контр.					
Утв.					

ГД-2026-003-АИ

Трёхкомнатная квартира

Общая площадь 78,95* м² · * размеры со скана, не замерены (реестр — л. 6–11, К-13)

Дизайн-проект интерьера трёхкомнатной квартиры

Стадия	Лист	Листов
РП	81	132

Кухня (пом. 6). Развёртка гарнитура

М 1:20

Кырлан Александр Сергеевич


выпуск 13.11.2026 № 6f3a8abb2c · стр. 89 из 157

Кухня (пом. 6). Развёртка гарнитура: вид без фасадов и разрезы


Кухня-гостиная (пом. 6) · стена В · вид из помещения · размеры в мм, отметки в м · лист 2: вид без фасадов, разрезы

ПРЕДВАРИТЕЛЬНО · не для производства работ · открыто пунктов: 28 (реестр — л. 6–11)


Вид без фасадов: наполнение, выводы (М 1:20)

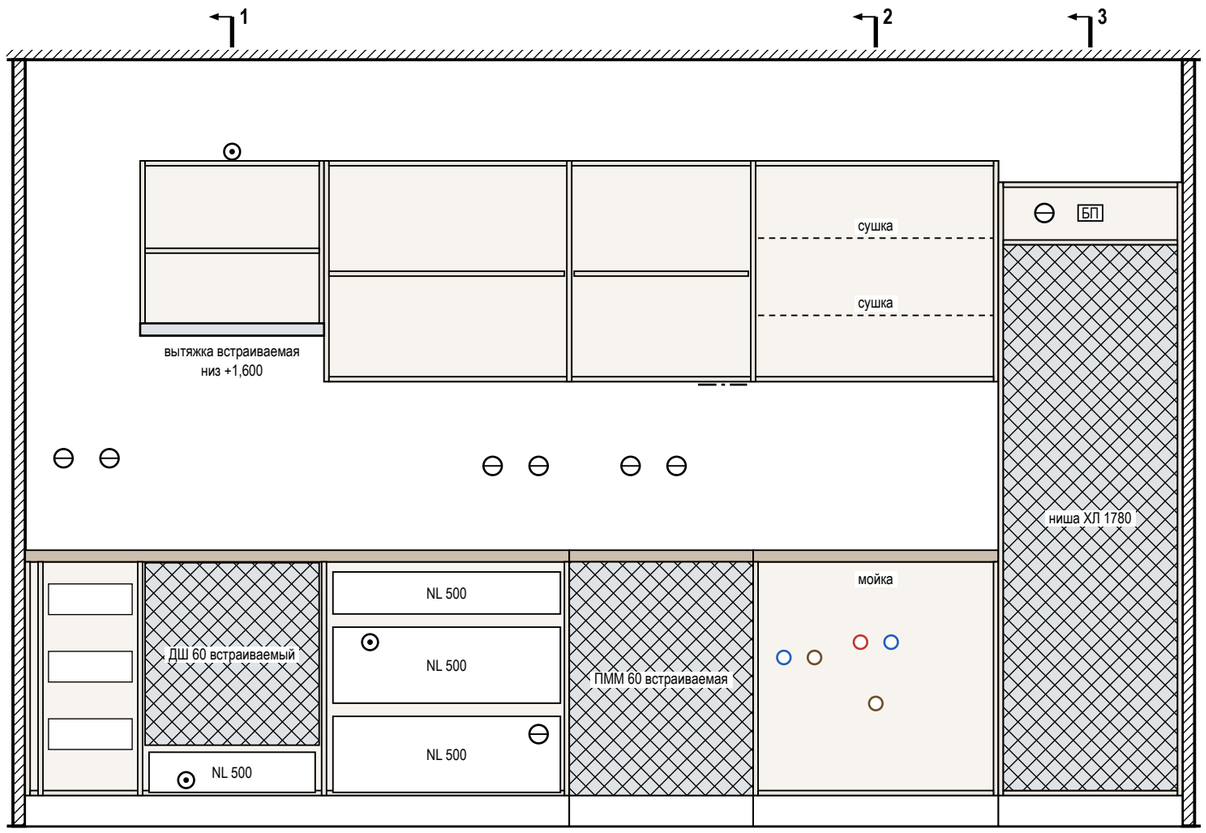


Разрез 1-1 (М 1:20)

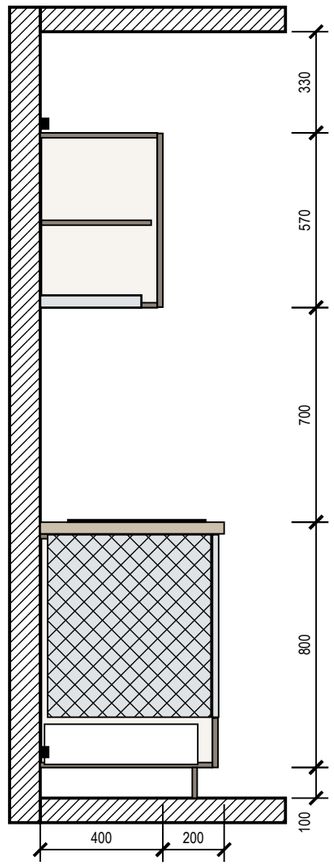

Разрез 2-2 (М 1:20)

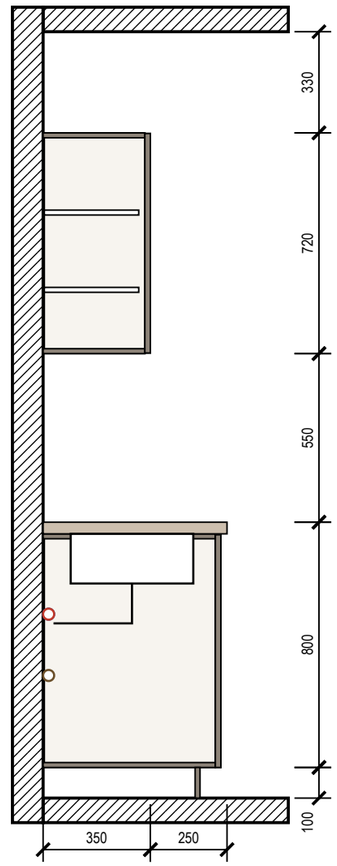

Разрез 3-3 (М 1:20)

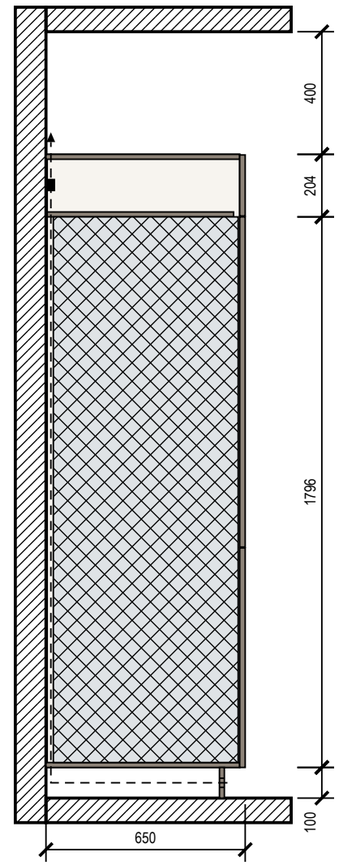

Примечания

1. Вытяжка встраивается в дно навесного модуля М15** над варочной: её низ на 1600 мм от пола, 700 мм над панелью (не меньше 650 мм).
2. Ниши техники (холодильник — ориентир 1780 мм) — по монтажным схемам выбранных моделей: решётка в цоколе и канал за пеналом холодильника, зазор за духовым шкафом, фасад ПММ на двери машины.
3. Допущение проекта: кухня: раскладка гарнитура принята проектной, решение автора (ИЗ-12) — мойка М7* у шахты Ш2, ПММ М14* рядом с мойкой, варочная и духовой шкаф в М8*, вытяжка М15**, холодильник М6**; выводы техники — по типовой расстановке; условие: до начала черновых работ сверить раскладку и выводы с чертежом кухни от изготовителя, выводы пересматриваются по его чертежу (вопрос К-8).
4. Марки из допущений, которых нет на этом листе: Ш2 — лист 48.

Допущения и предложения на листе

Основа листа: размеры сняты со скана плана заказчика по размерным цепочкам, контрольный обмер на объекте не выполнялся (К-13); высота потолка 2700 мм принята: на плане заказчика не указана (К-11); толщины стен приняты: наружные 250 мм, перегородки 150 мм (на плане 85–190 мм) (К-13); разрешённая мощность 15 кВт принята по типовой квартире, технических условий нет (К-14); утолщение стены 190 × 1360 мм и элемент 1470 × 160 мм плана заказчика не определены (К-12); ниши санузла 2 закрыты перегородкой и фальш-стеной: проектное решение, на плане заказчика ниша у входа открыта (К-18); несущие стены не определены: до технического заключения все существующие стены считаются несущими (К-20); окна существующие и сохраняются; подоконная доска и глубина откосов не заданы — приняты, не замерены (К-27); подрайон климата не задан — принят не северный (жилые от 2,5 м) (К-29).

Знак «*» — принято, не замерено и не подтверждено (замерить на объекте): К-8: М7, М14; М8 — Ряд М6…М8 стена-в-стену: было 600+800+600+1800 = 3800 от х 9730 до черновой грани стены Б (13530); чистовая длина стены по развёртке 3770 (отделка 15/15) — гарнитур длиннее стены на 30 мм, зазора под компенсатор нет.

Знак «**» — предложение проектировщика, заказчиком не утверждено (согласовать с заказчиком): ИЗ-5, К-8: М6, М15.

См. лист открытых вопросов (лист 6, запись К-8; лист 7, записи К-11–К-14, К-18, К-20; лист 8, записи К-27, К-29; лист 9, запись ИЗ-5).

1000 мм · печать 1:1

Изм.	Кол.уч	Лист	№ док.	Подп.	Дата
Разраб.		Кырлан А.С.			13.11.26
Пров.					
ГИП					
Н. контр.					
Утв.					

ГД-2026-003-АИ

Трёхкомнатная квартира

Общая площадь 78,95* м² · * размеры со скана, не замерены (реестр — л. 6–11, К-13)

Дизайн-проект интерьера трёхкомнатной квартиры

Стадия	Лист	Листов
РП	82	132

Кухня (пом. 6). Развёртка гарнитура: вид без фасадов и разрезы


М 1:20

Кырлан Александр Сергеевич


Кухня (пом. 6). Монтажная схема

Кухня-гостиная (пом. 6) · стена В · размеры в мм от чистых поверхностей, высоты — от чистого пола

Привязка выводов и крепление модулей (М 1:25)

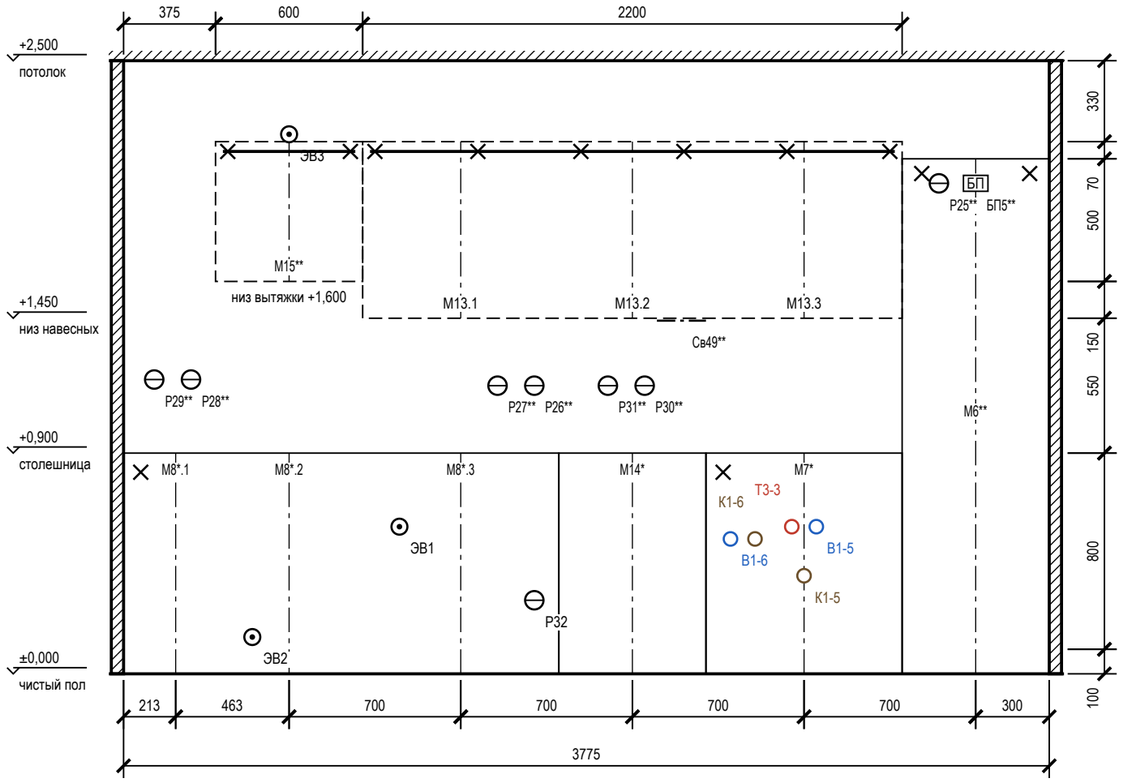

План столешницы (М 1:25)

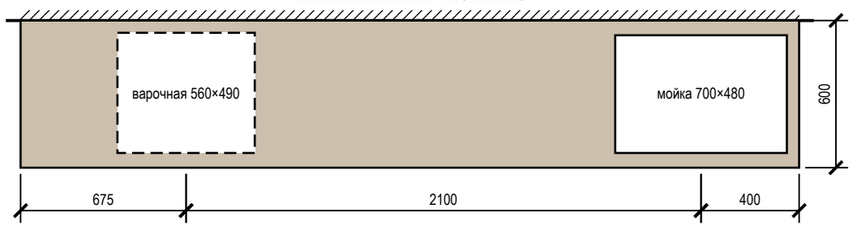

Привязка выводов к осям модулей

Код	Назначение	Модуль	От оси, мм	Н, мм	Размещение
Р29**	розетка — фартук	М8*.1	−87	1200	над столешницей (фартук)
Р28**	розетка ×2 — фартук	М8*.1	+63	1200	над столешницей (фартук)
ЭВ2	вывод кабеля — духовой шкаф	М8*.2	−150	150	под духовым шкафом, доступ через ящик
ЭВ3	вывод кабеля — вытяжка — над корпусом	М15**	0	2200	в навесном модуле
ЭВ1	вывод кабеля — варочная панель — за ящиком	М8*.3	−250	600	в соседнем модуле, за ящиком
Р27**	розетка — фартук	М8*.3	+150	1175	над столешницей (фартук)
Р26**	розетка ×2 — фартук	М8*.3	+300	1175	над столешницей (фартук)
Р32	розетка — посудомоечная машина	М8*.3	+300	300	в соседнем модуле, за ящиком
Р31**	розетка — фартук между мойкой и варочной	М14*	−100	1175	над столешницей (фартук)
Р30**	розетка ×2 — фартук между мойкой и варочной	М14*	+50	1175	над столешницей (фартук)
Св49**	светодиодная лента — подсветка столешницы	М14*	+200	1440	в профиле по низу навесного модуля
В1-6	В1 — кран ПММ в шкафу мойки	М7*	−300	550	в модуле мойки
К1-6	К1 Ø40 — слив ПММ в шкафу мойки	М7*	−200	550	в модуле мойки
Т3-3	Т3 — межос. 100	М7*	−50	600	в модуле мойки
К1-5	К1 Ø50 — мойка	М7*	0	400	в модуле мойки
В1-5	В1 — межос. 100	М7*	+50	600	в модуле мойки
Р25**	розетка — холодильник — в своём модуле, над нишей, за съёмной панелью	М6**	−150	2000	над нишей холодильника, съёмная панель
БП5**	блок питания — в пенале М6**, верх, съёмная панель	М6**	0	2000	над нишей холодильника, съёмная панель

Зазоры под отделку

Поверхность	Отделка	Зазор, мм	Учесть
фартук	керамогранит	10	от чернового основания до корпуса навесных и столешницы
стены	окраска	5	под штукатурку и шпаклёвку за пеналом
пол	инженерная доска		цоколь — после укладки пола, опоры ±20 мм

Условные обозначения

- нижний модуль, пенал (контур)
- невидимый контур: навесной модуль, корпус под столешницей
- ось модуля (от неё — привязка вывода)
- анкер / уголок крепления к стене
- розетка на стене
- вывод кабеля к технике
- В1 — вывод воды В1 / Т3, канализации К1

Примечания

1. Выводы — по проекту электрики и ВК; привязка по горизонтали — от оси модуля (плюс — вправо по виду), по высоте — от чистого пола до оси вывода.
2. Пенал — уголки к стене 2 шт. сверху; нижние модули — стяжками между собой и уголком к стене; ряд выставить по уровню опорами цоколя.
3. Розетки над столешницей — не ниже 150 мм над ней и не за корпусом техники; розетка за ПММ, духовым шкафом и холодильником — только в соседнем модуле или в зоне цоколя с доступом.
4. Столешница — вырезы по шаблонам выбранных моделей мойки и варочной панели; торцы у стены — герметик, пристеночный плинтус.
5. Допущение проекта: кухня: раскладка гарнитура принята проектной, решение автора (ИЗ-12) — мойка М7* у шахты Ш2, ПММ М14* рядом с мойкой, варочная и духовой шкаф в М8*, вытяжка М15**, холодильник М6**; выводы техники — по типовой расстановке; условие: до начала черновых работ сверить раскладку и выводы с чертежом кухни от изготовителя, выводы пересматриваются по его чертежу (вопрос К-8).
6. Марки из допущений, которых нет на этом листе: Ш2 — лист 48.

Допущения и предложения на листе. Основа листа: размеры сняты со скана плана заказчика по размерным цепочкам, контрольный обмер на объекте не выполнялся (К-13); высота потолка 2700 мм принята: на плане заказчика не указана (К-11); толщины стен приняты: наружные 250 мм, перегородки 150 мм (на плане 85–190 мм) (К-13); разрешённая мощность 15 кВт принята по типовой квартире, технических условий нет (К-14); утолщение стены 190 × 1360 мм и элемент 1470 × 160 мм плана заказчика не определены (К-12); ниши санузла 2 закрыты перегородкой и фальш-стеной: проектное решение, на плане заказчика ниша у входа открыта (К-18); несущие стены не определены: до технического заключения все существующие стены считаются несущими (К-20); окна существующие и сохраняются; подоконная доска и глубина откосов не заданы — приняты, не замерены (К-27); подрайон климата не задан — принят не северный (жилые от 2,5 м) (К-29). Знак «*» — принято, не замерено (замерить): К-8: М8. Знак «**» — предложено, не утверждено (согласовать): Р26, Р27, Р28, Р29, Р30, Р31; ИЗ-3: Св49, БП5; К-7, К-8: Р25. См. лист открытых вопросов (лист 6, записи К-7, К-8; лист 7, записи К-11–К-14, К-18, К-20; лист 8, записи К-24, К-27, К-29; лист 9, записи ИЗ-3, ИЗ-5).

1000 мм · печать 1:1

Изм.	Кол.уч	Лист	№ док.	Подп.	Дата
Разраб.		Кырлан А.С.			13.11.26
Пров.					
ГИП					
Н. контр.					
Утв.					

ГД-2026-003-АИ

Трёхкомнатная квартира

Общая площадь 78,95* м² · * размеры со скана, не замерены (реестр — л. 6–11, К-13)

Дизайн-проект интерьера трёхкомнатной квартиры

Стадия	Лист	Листов
РП	83	132

Кухня (пом. 6). Монтажная схема

М 1:25

Кырлан Александр Сергеевич


выпуск 13.11.2026 № 6f3a8abb2c · стр. 91 из 157

Кухня (пом. 6). Столешница: план

Кухня-гостиная (пом. 6) · размеры в мм · вид сверху

План столешницы (вид сверху, стена вверху) М 1:20

Ст-1: стена С, 3175×600

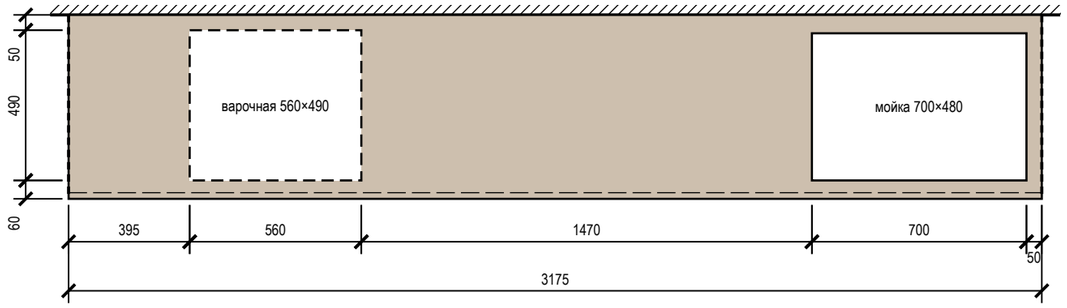

свес над фасадами 20 мм · толщина 38 мм*

Ведомость столешниц

Марка	Стена	Д×Ш×Т, мм	Материал	Вырезы	Кромка	Стыки
Ст-1	С	3175×600×38*	материал не задан (materials.worktop.mat	варочная 560×490; мойка 700×480	3,17 пог. м	нет
Итого			**S = 1,91 м²**		**3,17 пог. м**	

Примечания

1. Материал: материал не задан (materials.worktop.mat) (materials.worktop.mat в данных не задан); толщина 38 мм*.
2. * — толщина принята по практике (38 мм): в данных изделия materials.worktop.thk не задана.
3. Розеток в столешнице нет: питание над столешницей — на фартуке (план розеток), не за корпусом техники.
4. Вырезы: мойка — по габариту чаши 700×480 (прибор), отступ от стены 60 мм; варочная панель — ориентир 560×490 мм, отступ от стены 50 мм; вырезы разметить по шаблону выбранных моделей, углы выреза — радиус не менее 5 мм.
5. Радиусы углов и фаска кромки в данных не заданы: углы столешницы прямые, кромка — прямая без фаски, пока не задано иное.
6. Стыков нет: каждая столешница — одной деталью.
7. Свес над фасадами — 20 мм; торцы: свободный торец — кромка, торец у стены или пенала — зазор не более 3 мм, герметик. Длина кромки — по лицевой стороне и свободным торцам.

Допущения и предложения на листе

Основа листа: размеры сняты со скана плана заказчика по размерным цепочкам, контрольный обмер на объекте не выполнялся (К-13); высота потолка 2700 мм принята: на плане заказчика не указана (К-11); толщины стен приняты: наружные 250 мм, перегородки 150 мм (на плане 85–190 мм) (К-13); разрешённая мощность 15 кВт принята по типовой квартире, технических условий нет (К-14); утолщение стены 190 × 1360 мм и элемент 1470 × 160 мм плана заказчика не определены (К-12); ниши санузла 2 закрыты перегородкой и фальш-стеной: проектное решение, на плане заказчика ниша у входа открыта (К-18); несущие стены не определены: до технического заключения все существующие стены считаются несущими (К-20); окна существующие и сохраняются; подоконная доска и глубина откосов не заданы — приняты, не замерены (К-27); подрайон климата не задан — принят не северный (жилые от 2,5 м) (К-29).

См. лист открытых вопросов (лист 7, записи К-11–К-14, К-18, К-20; лист 8, записи К-27, К-29).

1000 мм · печать 1:1


						ГД-2026-003-АИ	
						Трёхкомнатная квартира	
						Общая площадь 78,95* м² · * размеры со скана, не замерены (реестр — л. 6–11, К-13)	
Изм.	Кол.уч	Лист	№ док.	Подп.	Дата	Дизайн-проект интерьера трёхкомнатной квартиры	Стадия: РП; Лист: 84; Листов: 132
Разраб.		Кырлан А.С.			13.11.26		
Пров.							
ГИП							
						Кухня (пом. 6). Столешница: план М 1:20	**Кырлан Александр Сергеевич**
Н. контр.							
Утв.							

выпуск 13.11.2026 № 6f3a8abb2c · стр. 92 из 157


Шкафы. Монтажная схема

крепление к стене, установочные размеры, зазоры под отделку · размеры в мм


Шкаф распашной С5 (пом. 1) (М 1:25)

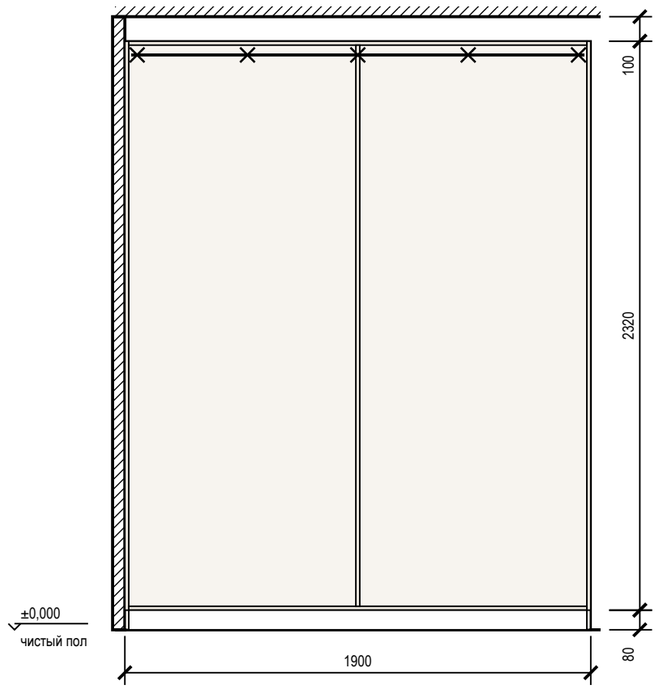

Система хранения Г1 (пом. 3) (М 1:25)**

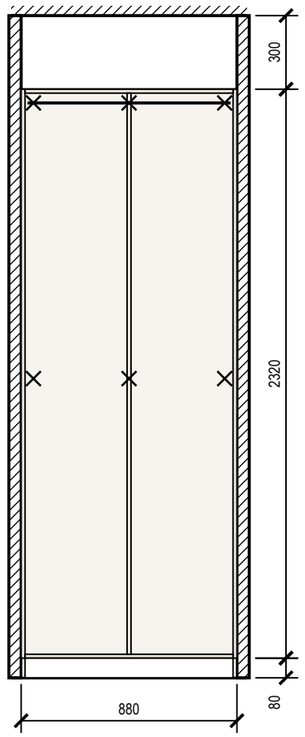

Шкаф-купе М16 (пом. 5) (М 1:25)

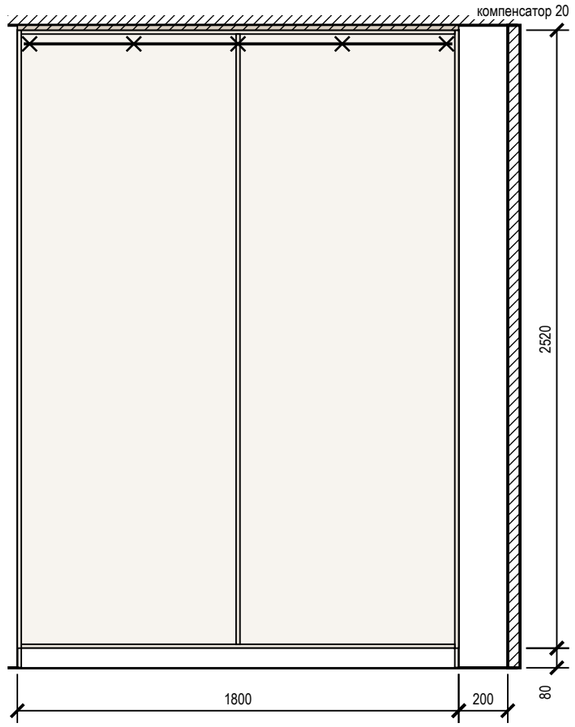

Допущения и предложения на листе

Основа листа: размеры сняты со скана плана заказчика по размерным цепочкам, контрольный обмер на объекте не выполнялся (К-13); высота потолка 2700 мм принята: на плане заказчика не указана (К-11); толщины стен приняты: наружные 250 мм, перегородки 150 мм (на плане 85–190 мм) (К-13); разрешённая мощность 15 кВт принята по типовой квартире, технических условий нет (К-14); утолщение стены 190 × 1360 мм и элемент 1470 × 160 мм плана заказчика не определены (К-12); ниши санузла 2 закрыты перегородкой и фальш-стеной: проектное решение, на плане заказчика ниша у входа открыта (К-18); несущие стены не определены: до технического заключения все существующие стены считаются несущими (К-20); окна существующие и сохраняются; подоконная доска и глубина откосов не заданы — приняты, не замерены (К-27); подрайон климата не задан — принят не северный (жилые от 2,5 м) (К-29).

Знак «**» — предложение проектировщика, заказчиком не утверждено (согласовать с заказчиком): К-9: Г1 — гардеробная 880 мм: система глубиной 600 вдоль длинной стены оставляла проход 280 мм — система перенесена на торцевую стену А, проход по всей ширине 880 мм.

См. лист открытых вопросов (лист 6, запись К-9; лист 7, записи К-11–К-14, К-18, К-20; лист 8, записи К-27, К-29).

Крепление и зазоры под отделку

Марка	Помещение, стена	Основание	Отделка стены	Зазор, мм	Крепёж по планке	От опрокидывания
С5	Спальня 1 (1), стена Б	по основанию — см. таблицу крепежа	окраска	5	анкер 5 шт., шаг 450	уголок к стене, 2 шт.
Г1**	Гардеробная (3), стена А	по основанию — см. таблицу крепежа	окраска	5	анкер 6 шт. (2 ряда)	крепление к стене, 3 точки
М16	Прихожая (5), стена Г	по основанию — см. таблицу крепежа	окраска	5	анкер 5 шт., шаг 425	уголки 2 шт.

Крепёж по основанию стены

Основание стены	Крепёж
бетон, ж/б	анкер-шуруп 7,5×72 или дюбель 8×60 с шурупом 5×70
кирпич полнотелый	дюбель 8×80 с шурупом 5×90
газобетон, пазогребень	дюбель для газобетона 10×100 или химический анкер
гипсокартон	закладная до обшивки (брус 40×80 или фанера 18 мм), саморез в закладную

Условные обозначения

- анкер / уголок крепления к стене
- корпус и полки ЛДСП (вид на стену)
- компенсатор — короб до потолка

Примечания

1. Установочные размеры — от чистого пола и чистых стен; перед установкой контрольный замер после отделки.
2. Порядок: корпус выставить по уровню опорами цоколя → закрепить к стене по задней планке → навесить двери и фасады, отрегулировать зазоры → подогнать и закрепить компенсатор.
3. Анкеры — с шагом не более 500 мм, не ближе 50 мм от края планки; на ГКЛ только в закладную, установленную до обшивки.
4. Скрытые коммуникации под анкеры проверить детектором; трассы электрики по плану розеток.
5. Сборка стоя на месте: М16 — корпус не собирается лёжа и не поднимается собранным, а собирается в проектном положении у стены; выставление по уровню и крепление к стене выполняются по корпусу, собранному на месте.

1000 мм · печать 1:1

Изм.	Кол.уч	Лист	№ док.	Подп.	Дата
Разраб.		Кырлан А.С.			13.11.26
Пров.					
ГИП					
Н. контр.					
Утв.					

ГД-2026-003-АИ

Трёхкомнатная квартира

Общая площадь 78,95* м² · * размеры со скана, не замерены (реестр — л. 6–11, К-13)

Дизайн-проект интерьера трёхкомнатной квартиры

Стадия	Лист	Листов
РП	85	132

Шкафы. Монтажная схема

М 1:25

Кырлан Александр Сергеевич

выпуск 13.11.2026 № 6f3a8abb2c · стр. 93 из 157

Ведомости изделий, техники и фурнитуры

встроенная мебель и кухонный гарнитур · размеры в мм

Ведомость изделий

Марка	Наименование	Пом.	Ш×Г×В, мм	Корпус	Фасад	Кромка, мм	Кол.
С5	Шкаф распашной	1	1900×600×2400	ЛДСП 16	МДФ 18 мм, эмаль матовая	0,4 / 2	1
Г1**	Система хранения	3	880×600×2400	ЛДСП 16	без фасадов	0,4 / 2	1
М16	Шкаф-купе	5	1800×600×2600	ЛДСП 16	ЛДСП 10 мм в алюминиевом профиле	0,4 / 2	1
М8*	Модуль нижний: карго, духовой шкаф, ящики, варочная	6	1775×600×900	ЛДСП 16	МДФ 18 мм, эмаль матовая	0,4 / 2	1
М15**	Модуль навесной: полки	6	600×400×570	ЛДСП 16	МДФ 18 мм, эмаль матовая	0,4 / 2	1
М13	Модуль навесной: полки, сушка	6	2200×350×720	ЛДСП 16	МДФ 18 мм, эмаль матовая	0,4 / 2	1
М14*	Модуль под ПММ 60: без корпуса, фасад на дверь машины	6	600×600×900	без корпуса	МДФ 18 мм, эмаль матовая — на дверь машины (навеска из её комплекта), цоколь		1
М7*	Модуль нижний: мойка	6	800×600×900	ЛДСП 16	МДФ 18 мм, эмаль матовая	0,4 / 2	1
М6**	Пенал: холодильник встр.	6	600×650×2100	ЛДСП 16	МДФ 18 мм, эмаль матовая	0,4 / 2	1

Ведомость встраиваемой техники

Поз.	Прибор	Ниша, вырез, мм	Вентиляция	Питание	Схема
М8*.2	Духовой шкаф встраиваемый, 60 см	ниша 560 × 600, глубина ≥ 550	зазор за шкафом, вырез в задней стенке	ЭВ2: М8*.2, H=150 — под духовым шкафом, доступ через ящик	по модели
М8*.2	Варочная панель индукционная, 60 см	вырез в столешнице 560 × 490		ЭВ1: М8*.3, H=600 — в соседнем модуле, за ящиком	по модели
М14*	Посудомоечная машина встраиваемая, 60 см	ниша 600 × 862 (от пола до низа столешницы)	зазор в цоколе, по схеме	Р32: М8*.3, H=300 — в соседнем модуле, за ящиком	по модели
М7*	Мойка врезная / подстольная с сифоном	вырез по шаблону, ориентир 700 × 480		смеситель — выводы ВК	по модели
М6**	Холодильник встраиваемый, ниша 1780	ниша 1780 × 560 × 550	решётка в цоколе, канал за корпусом, выход сверху	Р25**: М6**, H=2000 — над нишей холодильника, съёмная панель	по модели
М15**	Вытяжка встраиваемая в навесной модуль, 60 см	низ ≥ 650 над панелью	воздуховод к вентканалу, короб до потолка	ЭВ3: М15**, H=2200 — в навесном модуле	по модели

Ведомость фурнитуры

№	Фурнитура	Тип, размер	Изделия	Кол.
1	Петля накладная 110° с доводчиком	чашка 35 мм	С5, М15**, М13, М7*, М6**	51
2	Полкодержатель с фиксацией	ø5 мм	С5, Г1**, М16, М15**, М13, М6**	92
3	Штанга овальная 30×15, L = 926	+ 2 держателя	С5	1
4	Опора регулируемая с цоколем на клипсах	ход 20 мм	С5, Г1**, М16	22
5	Анкер по основанию стены	по таблице крепежа	С5, Г1**, М16, М15**, М13	24
6	Уголок крепления к стене от опрокидывания	стальной	С5, Г1**, М16, М6**	8
7	Штанга овальная 30×15, L = 416	+ 2 держателя	Г1**	1
8	Система дверей купе: профиль, направляющие, ролики	на 2 двери	М16	1
9	Ручка-профиль вертикальная	в цвет профиля	М16	2
10	Штанга овальная 30×15, L = 876	+ 2 держателя	М16	1
11	Полка для обуви выдвижная наклонная	ширина 876	М16	3
12	Карго выдвижное 3-уровневое	ширина 325	М8*	1
13	Направляющие полного выдвижения с доводчиком NL 500	пара	М8*	4
14	Ручка-профиль	латунь матовая	М8*, М15**, М13, М14*, М7*, М6**	19
15	Опора кухонная регулируемая 100–120 мм	+ клипса цоколя	М8*, М7*, М6**	16
16	Навес регулируемый для навесного шкафа	пара на секцию	М15**, М13	4
17	Шина монтажная	L = 540	М15**	1
18	Сушка для посуды в шкаф	ширина 800	М13	1
19	Шина монтажная	L = 2140	М13	1
20	Комплект навески фасада ПММ	из поставки машины	М14*	1

Допущения и предложения на листе

Основа листа: размеры сняты со скана плана заказчика по размерным цепочкам, контрольный обмер на объекте не выполнялся (К-13); высота потолка 2700 мм принята: на плане заказчика не указана (К-11); толщины стен приняты: наружные 250 мм, перегородки 150 мм (на плане 85–190 мм) (К-13); разрешённая мощность 15 кВт принята по типовой квартире, технических условий нет (К-14); утолщение стены 190 × 1360 мм и элемент 1470 × 160 мм плана заказчика не определены (К-12); ниши санузла 2 закрыты перегородкой и фальш-стеной: проектное решение, на плане заказчика ниша у входа открыта (К-18); несущие стены не определены: до технического заключения все существующие стены считаются несущими (К-20); окна существующие и сохраняются; подоконная доска и глубина откосов не заданы — приняты, не замерены (К-27); подрайон климата не задан — принят не северный (жилые от 2,5 м) (К-29).

Знак «*» — принято, не замерено и не подтверждено (замерить на объекте): К-8: М7, М14; М8 — Ряд М6…М8 стена-в-стену: было 600+800+600+1800 = 3800 от х 9730 до черновой грани стены Б (13530); чистовая длина стены по развёртке 3770 (отделка 15/15) — гарнитур длиннее стены на 30 мм, зазора под компенсатор нет.

Знак «**» — предложение проектировщика, заказчиком не утверждено (согласовать с заказчиком): И3-5, К-8: М6, М15; К-7, К-8: Р25 — высота 2000 мм выше нормы 1 м (ПУЭ 6.6.30) по назначению: питание встроенного холодильника М6, розетка над нишей за съёмной панелью; К-9: Г1 — гардеробная 880 мм: система глубиной 600 вдоль длинной стены оставляла проход 280 мм — система перенесена на торцевую стену А, проход по всей ширине 880 мм.

См. лист открытых вопросов (лист 6, записи К-7–К-9; лист 7, записи К-11–К-14, К-18, К-20; лист 8, записи К-27, К-29; лист 9, запись И3-5).

Примечания

1. Модели техники выбирает заказчик до изготовления мебели; ниши, вырезы и вентиляция — по монтажной схеме выбранной модели (условие гарантии), её номер вносится в ведомость.
2. Количество фурнитуры — по чертежам изделий; запас крепежа 5 %. Аналоги — по характеристикам (доводчик, нагрузка, ход).
3. Цвет корпусов, фасадов и профилей — по колерной карте проекта. Кромка — скрытые / видимые торцы, мм.
4. Допущение проекта: кухня: раскладка гарнитура принята проектной, решение автора (И3-12) — мойка М7* у шахты Ш2, ПММ М14* рядом с мойкой, варочная и духовой шкаф в М8*, вытяжка М15**, холодильник М6**; выводы техники — по типовой расстановке; условие: до начала черновых работ сверить раскладку и выводы с чертежом кухни от изготовителя, выводы пересматриваются по его чертежу (вопрос К-8).
5. Марки из допущений, которых нет на этом листе: Ш2 — лист 48.

Изм.	Кол.уч	Лист	№ док.	Подп.	Дата
Разраб.		Кырлан А.С.			13.11.26
Пров.					
ГИП					
Н. контр.					
Утв.					

ГД-2026-003-АИ

Трёхкомнатная квартира

Общая площадь 78,95* м² · * размеры со скана, не замерены (реестр — л. 6–11, К-13)

Дизайн-проект интерьера трёхкомнатной квартиры

Стадия	Лист	Листов
РП	86	132

Ведомости изделий, техники и фурнитуры

М б/м

Кырлан Александр Сергеевич

выпуск 13.11.2026 № 6f3a8abb2c · стр. 94 из 157

Сводка листовых материалов и кромки

ЛДСП, МДФ, ХДФ и кромка по изделиям · площади в м², кромка в пог. м

Листовые материалы по толщинам и декорам

Материал, декор	Назначение	Изделий	S, м²	S × 1,15*, м²
ЛДСП 16 мм*	корпус	8	37,26	42,85
ХДФ 4 мм	задняя стенка	8	16,07	18,48
МДФ 18 мм, эмаль матовая	фасад	7	9,49	10,91
ЛДСП 10 мм в алюминиевом профиле	фасад	1	4,40	5,06
Итого			**67,23**	**77,31**

Кромка по типам

Кромка	Толщина, мм	Длина, пог. м	+10 %*, пог. м
видимая (передний торец, торец фасада ЛДСП)	2	93,4	102,7
скрытая (задний торец деталей корпуса)	0,4	67,3	74,0

Изделия (9)

Изделие	Пом.	Корпус, м²	ХДФ, м²	Фасад, м²	Кромка, пог. м
С5 Шкаф распашной	1	9,46	4,41	4,37	34,3
Г1** Система хранения	3	6,68	2,04	0,00	23,1
М16 Шкаф-купе	5	9,70	4,54	4,40	49,5
М8* модуль кухни	6	2,36	1,35	0,98	11,8
М15** модуль кухни	6	1,08	0,34	0,34	5,7
М13 модуль кухни	6	2,81	1,58	1,56	17,3
М14* модуль кухни	6	0,00	0,00	0,45	0,0
М7* модуль кухни	6	1,52	0,61	0,60	6,9
М6** модуль кухни	6	3,65	1,20	1,19	12,0

Примечания

1. Площади — по моделям изделий листов мебельщика: боковины, дно, крыша (у нижнего кухонного модуля — дно и две царги по 100 мм), полки, стойки, задняя стенка ХДФ, цоколь, фасады. Коэффициент раскроя 1,15* — обрезь, пропилы и подбор рисунка; сводка — для заказа материала, раскрой делает цех.
2. Кромка: видимая — передний торец деталей корпуса и периметр фасада из ЛДСП; скрытая — задний торец деталей корпуса. Фасады из МДФ (эмаль, шпон) кромки не имеют. Толщина — из materials.edge изделий; где не задана — по умолчанию 2 и 0,4 мм*.
3. Не вошло: короба ящиков (в комплекте направляющих NL), столешница (лист «Столешница: план» и раскрой камня), остров, встроенная техника, покупные изделия.
4. Мягкое изголовье С1 (пом. 1), С7 (пом. 4): чертёж не выпущен — в данных нет ширина панели, высота панели, толщина панели, членение и стёжка (шаг, рисунок) или «гладкая обивка» (plain), ткань (headboardSpec.fabric) (записи реестра нет).
5. * — значение принято по практике, не задано в данных.

Допущения и предложения на листе

Основа листа: размеры сняты со скана плана заказчика по размерным цепочкам, контрольный обмер на объекте не выполнялся (К-13); высота потолка 2700 мм принята: на плане заказчика не указана (К-11); толщины стен приняты: наружные 250 мм, перегородки 150 мм (на плане 85–190 мм) (К-13); разрешённая мощность 15 кВт принята по типовой квартире, технических условий нет (К-14); утолщение стены 190 × 1360 мм и элемент 1470 × 160 мм плана заказчика не определены (К-12); ниши санузла 2 закрыты перегородкой и фальш-стеной: проектное решение, на плане заказчика ниша у входа открыта (К-18); несущие стены не определены: до технического заключения все существующие стены считаются несущими (К-20); окна существующие и сохраняются; подоконная доска и глубина откосов не заданы — приняты, не замерены (К-27); подрайон климата не задан — принят не северный (жилые от 2,5 м) (К-29).

Знак «*» — принято, не замерено и не подтверждено (замерить на объекте): К-8: М7, М14; М8 — Ряд М6…М8 стена-в-стену: было 600+800+600+1800 = 3800 от х 9730 до черновой грани стены Б (13530); чистовая длина стены по развёртке 3770 (отделка 15/15) — гарнитур длиннее стены на 30 мм, зазора под компенсатор нет.

Знак «**» — предложение проектировщика, заказчиком не утверждено (согласовать с заказчиком): ИЗ-2, К-2, К-23: пол пом. 2, 7 — пирог пола: стяжка 33 мм и обмазочная гидроизоляция добавлены разработчиком проекта; артикул изделия не выбран: позиция описана характеристиками («аналог по характеристикам»), артикул выбирается при закупке; ИЗ-5, К-8: М6, М15; К-2, К-23: стены пом. 2, 7 — артикул изделия не выбран: позиция описана характеристиками («аналог по характеристикам»), артикул выбирается при закупке; К-9: Г1 — гардеробная 880 мм: система глубиной 600 вдоль длинной стены оставляла проход 280 мм — система перенесена на торцевую стену А, проход по всей ширине 880 мм; К-23: пол пом. 1, 3–6, 8, плинтус пом. 1, 3–6, 8, фартук пом. 6 — артикул изделия не выбран: позиция описана характеристиками («аналог по характеристикам»), артикул выбирается при закупке.

См. лист открытых вопросов (лист 6, записи К-2, К-8, К-9; лист 7, записи К-11–К-14, К-18, К-20; лист 8, записи К-23, К-27, К-29; лист 9, записи ИЗ-2, ИЗ-5).

Изм.	Кол.уч	Лист	№ док.	Подп.	Дата
Разраб.		Кырлан А.С.			13.11.26
Пров.					
ГИП					
Н. контр.					
Утв.					

ГД-2026-003-АИ

Трёхкомнатная квартира

Общая площадь 78,95* м² · * размеры со скана, не замерены (реестр — л. 6–11, К-13)

Дизайн-проект интерьера трёхкомнатной квартиры

Стадия	Лист	Листов
РП	87	132

Сводка листовых материалов и кромки

М б/м

Кырлан Александр Сергеевич

выпуск 13.11.2026 № 6f3a8abb2c · стр. 95 из 157

09

Развёртки и узлы



Кырлан Александр Сергеевич

выпуск 13.11.2026 · 6f3a8abb2c · стр. 96 из 157

Реестр марок отделки и позиций альбома

Реестр марок отделки (О ↔ позиции колерной карты) и марки позиций по видам

Реестр марок отделки альбома

Марка	Поверхность	Материал, изделие	Цвет, код	Помещения	Колер. карта
О1	стены	окраска, Farrow & Ball Modern Emulsion, матовая, подготовка Q3	Farrow & Ball No. 241 «Skimming Stone»	1, 4, 5, 6, 8	К1
О2	акцентная стена	окраска, Farrow & Ball Modern Emulsion, матовая, подготовка Q3	Farrow & Ball No. 30 «Hague Blue»	1, 4, 6	К2
О3	плинтус	плинтус МДФ, h 80 мм, аналог: плинтус МДФ под покраску 80×16	Farrow & Ball No. 241 «Skimming Stone»	1, 4, 5, 6, 8	К4
О4	потолок	окраска, Tikkurila Anti-Reflex 2, глубокоматовая, подготовка Q3	Tikkurila V503 «Winter»	1, 3, 4, 5, 6, 8	К3
О5	пол	инженерная доска, аналог: инженерная доска, дуб натуральный, масло, 1-полосная, 14/4 мм		1, 3, 4, 6, 8	КМ1
О6	стены	облицовка плиткой, 600×1200×9 мм, аналог: керамогранит под травертин, матовый, затирка CG2WA		2, 7	КМ2
О7	потолок	окраска, Tikkurila Luja 7, матовая, подготовка Q3	Tikkurila V503 «Winter»	2, 7	К5
О8	пол	керамогранит, 600×600×9 мм, аналог: керамогранит ректифицированный под травертин, матовый, затирка CG2WA		2, 7	КМ3
О9	стены	окраска, Tikkurila Harmony, матовая, подготовка Q3	Tikkurila V503 «Winter»	3	К6
О10	плинтус	плинтус МДФ, h 80 мм, аналог: плинтус МДФ под покраску 80×16	Tikkurila V503 «Winter»	3	К7
О11	пол	керамогранит, 600×1200×9 мм, аналог: керамогранит ректифицированный под травертин, матовый, затирка CG2WA		5	КМ4
О12	фартук	керамогранит, 1200×600×9 мм, аналог: керамогранит под травертин, матовый, затирка CG2WA		6	КМ5

Марки позиций альбома по видам

Префикс	Что обозначает, позиции	Листы
Д	двери: Д-1–Д-5	27–30
ПР	проёмы без полотна (порталы): ПР-1, ПР-2	27–30
ОК	окна: ОК-1–ОК-4	27–30
Г, М, С	мебель и оборудование: Г1**, М1**, М2–М5, М6**, М7*, М8*, М13, М14*, М15**, М16, М17, М18**, С1–С11, С12**	31–36
П	сантехнические приборы: П1–П3, П4*, П6–П8, П10**, П11*, П12*, П13**	48–56
ДК	декор (картины, зеркала, растения): ДК1–ДК9, ДК10**, ДК11**, ДК12**, ДК13**, ДК14**, ДК15**, ДК16**, ДК17**, ДК18**, ДК19**, ДК20**, ДК21**, ДК22**, ДК23**, ДК24**, ДК25**	1, 71–76
Т	текстиль (шторы, ковры): Т1–Т19, Т20**, Т21**, Т22**, Т23**, Т24**, Т25**	1, 71–76
S	выключатели: S1–S10, S11**, S12**, S13–S16, S17**, S18**	37–45
Р	розетки: Р1–Р6, Р7**, Р8**, Р9–Р11, Р12**, Р13–Р16, Р17**, Р18**, Р19**, Р20–Р24, Р25**, Р26**, Р27**, Р28**, Р29**, Р30**, Р31**, Р32, Р33**, Р34	37–45
LAN	розетки компьютерные: LAN1–LAN3	37–45

Марки позиций альбома по видам (продолжение)

Префикс	Что обозначает, позиции	Листы
Св	светильники: Св1–Св14, Св15**, Св16–Св29, Св30**, Св31**, Св32**, Св33**, Св34**, Св35**, Св36**, Св37**, Св38**, Св39**, Св40**, Св41, Св42**, Св43**, Св44**, Св45–Св48, Св49**, Св50, Св51, Св52**, Св53, Св54	37–45
БП	блоки питания LED: БП1–БП4, БП5**	37–45
ИП	извещатели: ИП1–ИП6	37–45
ЭВ	выводы кабеля: ЭВ1–ЭВ3, ЭВ4**, ЭВ5**, ЭВ6**, ЭВ7**	37–45
КУП	электроустановочные изделия: КУП1**, КУП2**	37–45
ТВ	розетки ТВ: ТВ1, ТВ2	37–45
ЩК, ЩС**	щиты: ЩК, ЩС**	37–45
ДФ	домофон: ДФ1	37–45
АР	точки доступа Wi-Fi: АР1**, АР2**	37–45
Ст В1, Ст К1	стояки (системы В1, Т3, К1): Ст В1-1*, Ст В1-2*, Ст К1-1*, Ст К1-2*	48–56
Ш	шахты и короба: Ш1, Ш2	27–30
О	марки отделки (реестр альбома): О1–О12	2–5, 88–115
К, КМ	позиции колерной карты: К1–К7, КМ1–КМ5	69, 70
РО	радиаторы отопления: РО-1–РО-4	46, 47

Примечания

1. Марка отделки О — одна на весь альбом: одна и та же отделка (материал, изделие, цвет, формат) на всех листах имеет одну марку; на развёртках и планах стоят марки этого реестра.
2. Столбец «Колер. карта» — позиции колерной карты (лист 69): К — окраска по коду цвета, КМ — материал без кода цвета; «Помещения» — номера по экспликации; количества — по ведомости отделки помещений (лист 67).
3. Марки позиций: один префикс — один вид позиций на весь альбом (двери Д, окна ОК, мебель М, сантехприборы П, декор ДК, текстиль Т, колерная карта К и КМ, радиаторы РО, розетки Р, выключатели S, светильники Св; стояки — «Ст» и система, например «Ст К1-1*»). Совпадение префиксов у разных видов — замечание к исходным данным, при выпуске исправляется в модели.

Допущения и предложения на листе. Основа листа: размеры сняты со скана плана заказчика по размерным цепочкам, контрольный обмер на объекте не выполнялся (К-13); высота потолка 2700 мм принята: на плане заказчика не указана (К-11); толщины стен приняты: наружные 250 мм, перегородки 150 мм (на плане 85–190 мм) (К-13); разрешённая мощность 15 кВт принята по типовой квартире, технических условий нет (К-14); утолщение стены 190 × 1360 мм и элемент 1470 × 160 мм плана заказчика не определены (К-12); ниши санузла 2 закрыты перегородкой и фальш-стеной: проектное решение, на плане заказчика ниша у входа открыта (К-18); несущие стены не определены: до технического заключения все существующие стены считаются несущими (К-20); окна существующие и сохраняются; подоконная доска и глубина откосов не заданы — приняты, не замерены (К-27); подрайон климата не задан — принят не северный (жилые от 2,5 м) (К-29). Знак «*» — принято, не замерено (замерить): ИЗ-11, К-19: П4; К-8: М8, П11. Знак «**» — предложено, не утверждено (согласовать): Св15, Св30, S17, S18, Р26, Р27, Р28, Р29, Р30, Р31, Св31, Св32, Св33, Св34, Св35, Св36, Св37, Св38, Св39, Св40, Св52; ИЗ-1: ЭВ6, ЭВ7; ИЗ-2, К-2, К-23: пол пом. 2, 7; ИЗ-3: S11, S12, Св42, Св43, Св44, Св49, БП5; ИЗ-6: М1; ИЗ-8: ЭВ4, КУП1, ЭВ5, КУП2; ИЗ-9, ИЗ-17, К-7: ЩС; ИЗ-17: АР1, АР2; ИЗ-20: М18; К-2, К-23: стены пом. 2, 7; К-7: С12, Р12, Р17, Р18, Р19; К-7, К-8: Р25; К-9: Г1; К-23: пол пом. 1, 3–6, 8, плинтус пом. 1, 3–6, 8, фартук пом. 6. См. лист открытых вопросов (лист 6, записи К-2, К-7–К-9; лист 7, записи К-11–К-14, К-17–К-20; лист 8, записи К-23, К-27, К-29; лист 9, записи ИЗ-1–ИЗ-6, ИЗ-8, ИЗ-9; лист 10, записи ИЗ-11, ИЗ-15; лист 11, записи ИЗ-17, ИЗ-20).

Изм.	Кол.уч	Лист	№ док.	Подп.	Дата	ГД-2026-003-АИ			
						Трёхкомнатная квартира			
						Общая площадь 78,95* м² · * размеры со скана, не замерены (реестр — л. 6–11, К-13)			
Разраб.		Кырлан А.С.			13.11.26	Дизайн-проект интерьера трёхкомнатной квартиры	Стадия	Лист	Листов
Пров.							РП	88	132
ГИП									
Н. контр.						Реестр марок отделки и позиций альбома	Кырлан Александр Сергеевич		
Утв.						М б/м			

выпуск 13.11.2026 № 6f3a8abb2c · стр. 97 из 157

Схема расположения развёрток и узлов

План квартиры: марки развёрток по помещениям, выноски узлов, ведомость «марка → лист»

ПРЕДВАРИТЕЛЬНО · не для производства работ · открыто пунктов: 28 (реестр — л. 6–11)



Развёртки и узлы: марка → лист

Марка	Помещение / узел	Лист
А	Спальня 1 (пом. 1)	90
Б	Спальня 1 (пом. 1)	91
В	Спальня 1 (пом. 1)	92
Г	Спальня 1 (пом. 1)	93
А, Б	Ванная (пом. 2)	94
В, Г	Ванная (пом. 2)	95
А, Б	Гардеробная (пом. 3)	96
В, Г	Гардеробная (пом. 3)	97
А	Спальня 2 (пом. 4)	98
Б	Спальня 2 (пом. 4)	99
В	Спальня 2 (пом. 4)	100
Г	Спальня 2 (пом. 4)	101
А	Прихожая (пом. 5)	102
Б, В	Прихожая (пом. 5)	103
Г	Прихожая (пом. 5)	104
Б2	Кухня-гостиная (пом. 6)	105
В1	Кухня-гостиная (пом. 6)	106
А	Кухня-гостиная (пом. 6)	107
Б1, В2	Кухня-гостиная (пом. 6)	108
Г1**, Г2	Кухня-гостиная (пом. 6)	109
А, Б	Санузел 2 (пом. 7)	110
В, Г	Санузел 2 (пом. 7)	111
А, Б	Коридор (пом. 8)	112
В, Г	Коридор (пом. 8)	113
узел 1	Порог 15 мм: мокрая зона — смежное помещение	114
узел 2	Стык покрытий пола Т-профилем без перепада	114
узел 3	Дверь скрытого монтажа в плоскости стены, плинтус	114
узел 4	Короб стояков К1-1, В1-1 с люком и звукоизоляцией	114
узел 5	Гидроизоляция санузла: заход на стены 200 мм, примыкание ванны	115
узел 6	Плинтус МДФ 80×16 мм у окрашенной стены по доске (ламинату)	115
узел 7	Плинтус МДФ 80×16 мм у окрашенной стены по керамограниту (плитке)	115

Условные обозначения

- (А) — марка развёртки: буква стены, стрелка — взгляд
- выноска узла: над полкой — узел, под полкой — лист
- (1) — номер помещения, площадь м²

Примечания

1. Развёртки — вид на стену изнутри помещения; буквы стен — одна система на весь альбом (как на листах выводов, плитки и отделки).
2. Стены без электроточек, мебели, декора и акцентной отделки развёрток не имеют: их отделка — по ведомости отделки помещений.
3. Узлы — на листе узлов; места применения — по выноскам этого листа и ведомости «марка → лист».

Допущения и предложения на листе. Знак «*» принято (замерить): Ст К1-1, Ст В1-1, Ст К1-2, Ст В1-2. Знак «**» предложено (согласовать). См. лист открытых вопросов (листы 6–11).

1000 мм · печать 1:1

Изм.	Кол.уч	Лист	№ док.	Подп.	Дата
Разраб.		Кырлан А.С.			13.11.26
Пров.					
ГИП					
Н. контр.					
Утв.					

ГД-2026-003-АИ

Трёхкомнатная квартира

Общая площадь 78,95* м² · * размеры со скана, не замерены (реестр — л. 6–11, К-13)

Дизайн-проект интерьера трёхкомнатной квартиры

Стадия	Лист	Листов
РП	89	132

Схема расположения развёрток и узлов

М 1:50

Кырлан Александр Сергеевич


выпуск 13.11.2026 № 6f3a8abb2c · стр. 98 из 157

Развёртка стены А. Спальня 1 (пом. 1)

Спальня 1 (пом. 1) · вид изнутри помещения · размеры в мм, отметки в м

ПРЕДВАРИТЕЛЬНО · не для производства работ · открыто пунктов: 28 (реестр — л. 6–11)

Стена А (М 1:25)

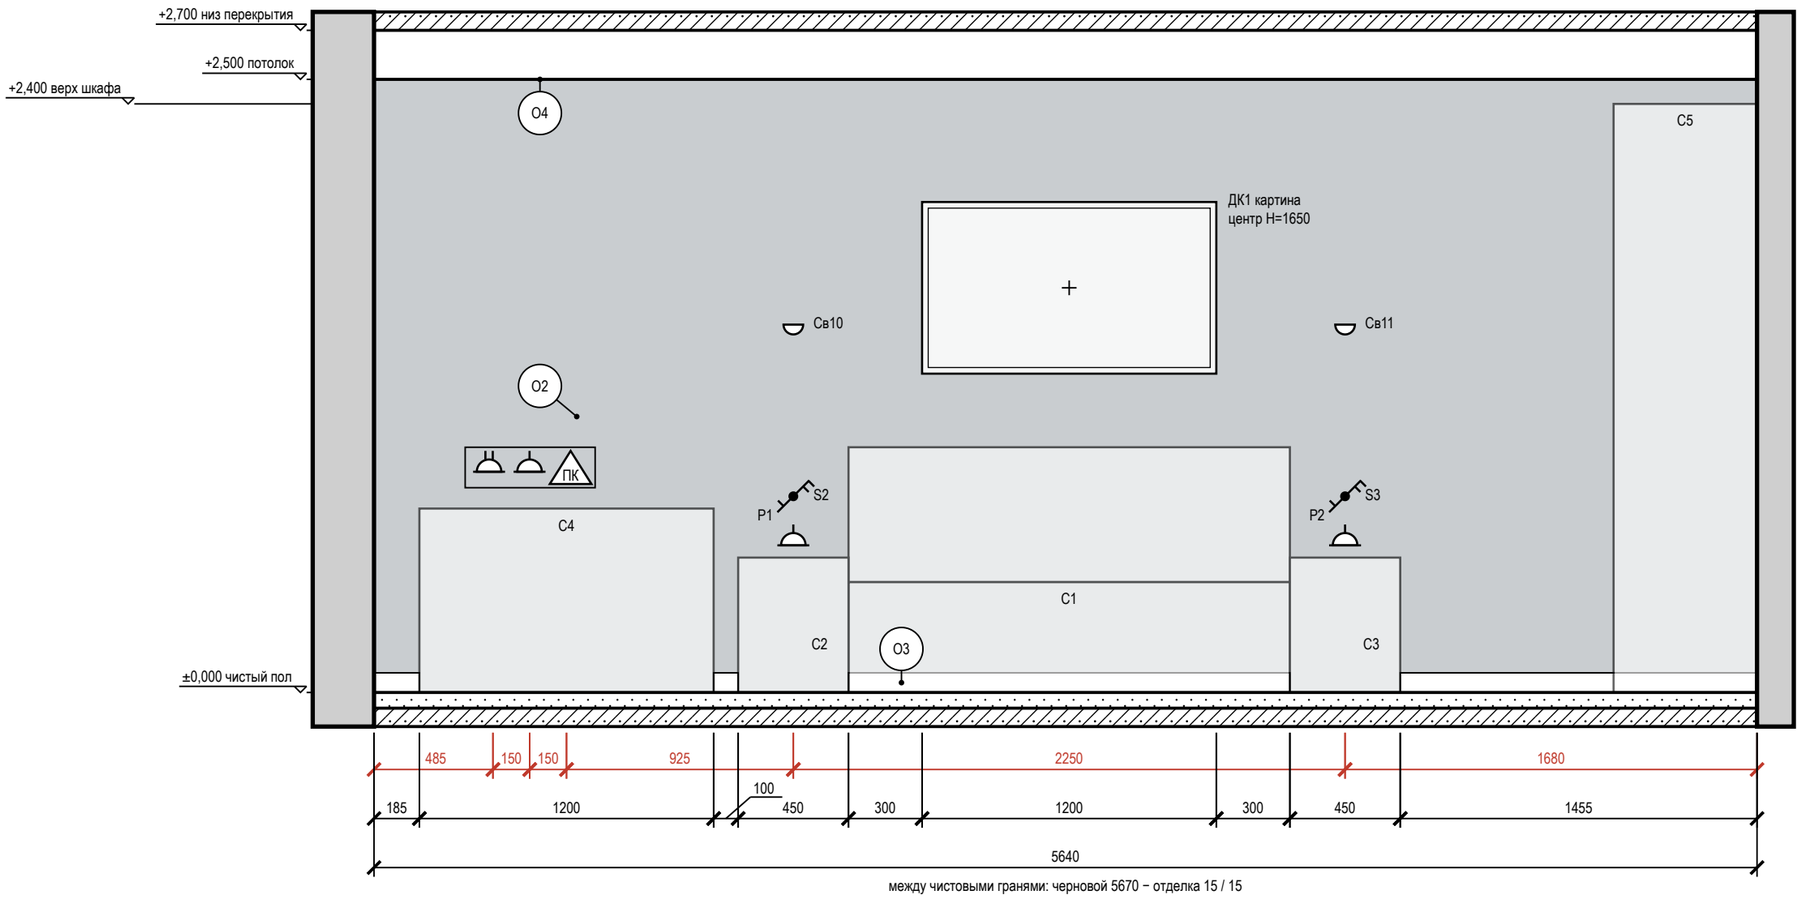


между чистовыми гранями: черновой 5670 − отделка 15 / 15

Условные обозначения

- розетка с заземляющим контактом; у знака марка, ×N — постов в рамке, гр. — группа щита, Н — высота оси, мм
- выключатель одноклавишный
- выключатель двухклавишный (флажков — по числу клавиш)
- выключатель с проходной или перекрёстной клавишей (обратный флажок); тип клавиши — в подписи
- светильник настенный (бра), Н — высота оси
- розетка компьютерная RJ45
- привязки точек и выводов от угла и от пола, мм
- мебель и приборы — фасад по расстановке (условно)
- картина (декор): марка Д, крест — центр, Н — высота центра, мм
- стены и перекрытия в сечении
- окраска: тон — цвет по коду производителя (условно)
- О1 — марка отделки по реестру отделки альбома
- А — марка развёртки: буква стены, стрелка взгляд

Схема развёрток (М 1:100)

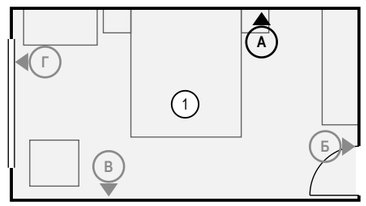

Ведомость точек и выводов

Марка	Что это	Гр.	Н, мм	От угла, мм	Примечание
Р3	розетка: рабочий стол	4	900	485	рамка 2 поста
Р4	розетка: рабочий стол	4	900	635	
LAN1	розетка RJ45: рабочий стол		900	785	
Р1	розетка: у кровати	4	600	1710	
S2	выключатель	1	800	1710	

Марка	Что это	Гр.	Н, мм	От угла, мм	Примечание
Св10	светильник настенный	1	1500	1710	
Р2	розетка: у кровати	4	600	3960	
S3	выключатель	1	800	3960	
Св11	светильник настенный	1	1500	3960	

Примечания

1. Развёртки — вид на стену изнутри помещения, по часовой стрелке; расположение — на схеме листа и на листе 89; размеры — в мм по чистовым поверхностям; отметки — в м от ±0,000; высоты Н — от чистого пола помещения до оси изделия, у декора — до центра.
2. Красная цепочка — привязки электроточек и выводов по осям от угла чистовых стен; высота Н — у знака, от чистого пола до оси; высоты мебели, проёмов и границ отделки — колонкой отметок слева. У знака — короткая марка; назначение, группа щита, высота и привязка каждой точки и вывода — в «Ведомости точек и выводов» под видами (каждая точка — строка).
3. Отделка стен — по ведомости отделки помещений, лист 67.
4. У знака электроточки: марка (Р — розетка, S — выключатель, Св — светильник, ЭВ — вывод кабеля), ×N — число постов в рамке, гр. — группа щита, Н — высота оси от чистого пола, мм; группы по клавишам выключателя — на листе выключателей.
5. Схема мебели, приборов и декора не является технической документацией для производства мебели; габариты — по паспортам изделий.
6. Картины и зеркала крепить к основанию по паспорту изделия (закладные и анкеры — в перечне скрытых работ); крест — ось центра предмета.
7. Потолок — у каждой стены свой, по плану потолков (ПТ1); ступени — зоной, кромка короба перед нишей — тонкой линией; в поле потолка: ПТ2 +2,600.
8. Часть марок не уместилась у знаков: коды, высоты и привязки этих позиций — в ведомости точек и выводов под видами.

Допущения и предложения на листе. Знак «*» принято (замерить): отметка существующего пола. См. лист открытых вопросов (листы 6–11).

1000 мм · печать 1:1

Изм.	Кол.уч	Лист	№ док.	Подп.	Дата
Разраб.		Кырлан А.С.			13.11.26
Пров.					
ГИП					
Н. контр.					
Утв.					

ГД-2026-003-АИ

Трёхкомнатная квартира

Общая площадь 78,95* м² · * размеры со скана, не замерены (реестр — л. 6–11, К-13)

Дизайн-проект интерьера трёхкомнатной квартиры

Стадия	Лист	Листов
РП	90	132

Развёртка стены А. Спальня 1 (пом. 1)

М 1:25

Кырлан Александр Сергеевич


выпуск 13.11.2026 № 6f3a8abb2c · стр. 99 из 157

Развёртка стены Б. Спальня 1 (пом. 1)

Спальня 1 (пом. 1) · вид изнутри помещения · размеры в мм, отметки в м

ПРЕДВАРИТЕЛЬНО · не для производства работ · открыто пунктов: 28 (реестр — л. 6–11)

Стена Б (М 1:20)

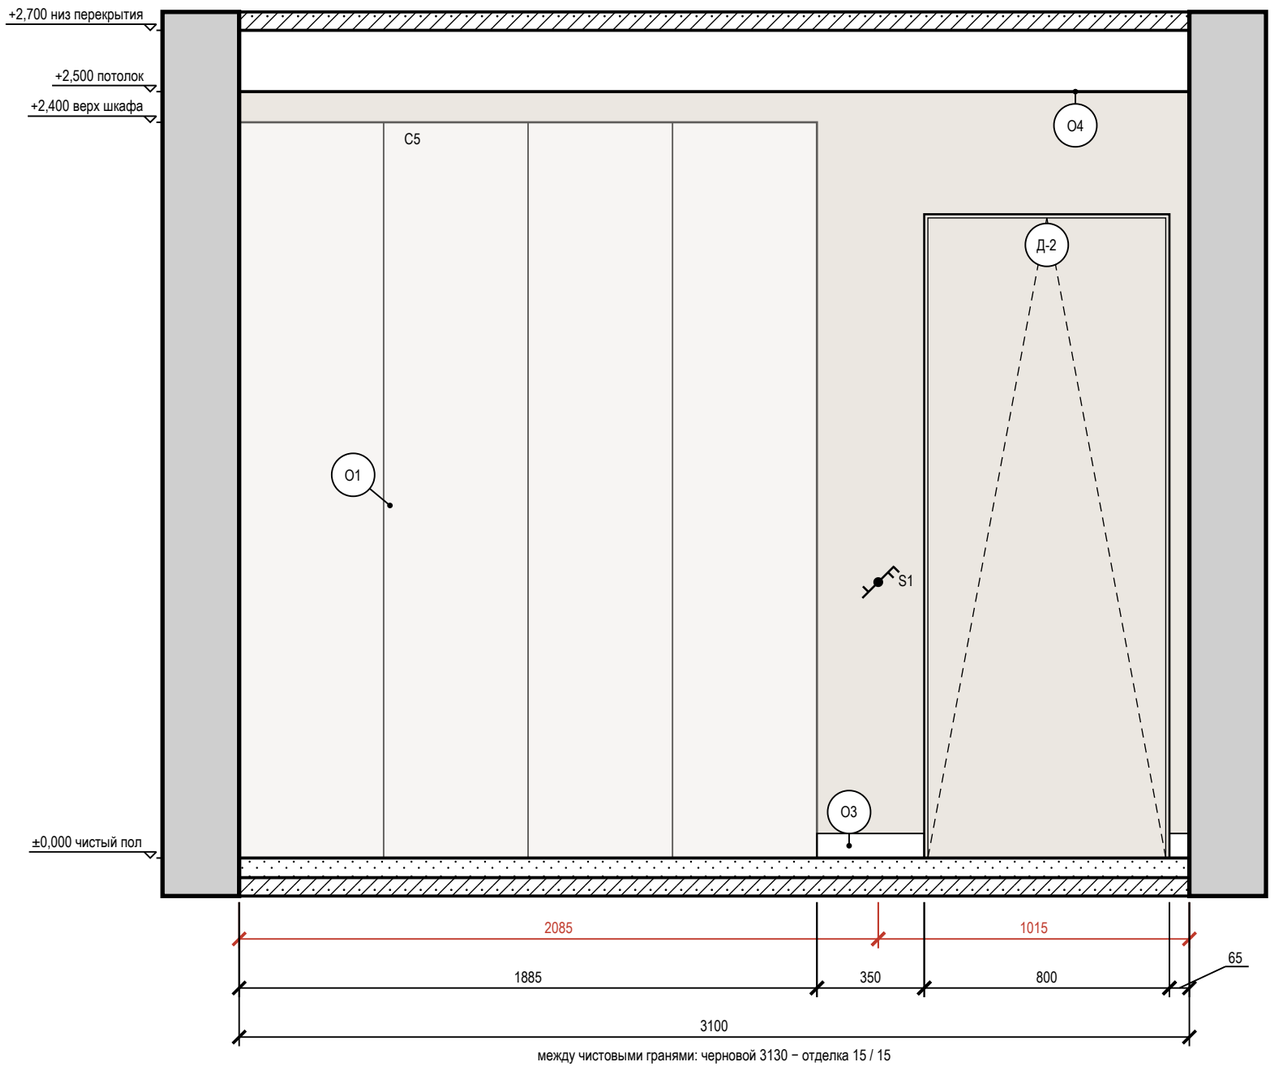

Ведомость точек и выводов

Марка	Что это	Гр.	Н, мм	От угла, мм	Примечание
S1	выключатель	1	900	2085	


Условные обозначения

- выключатель одноклавишный
- выключатель двухклавишный (флажков — по числу клавиш)
- выключатель с проходной или перекрёстной клавишей (обратный флажок); тип клавиши — в подписи
- привязки точек и выводов от угла и от пола, мм
- мебель и приборы — фасад по расстановке (условно)
- дверь скрытого монтажа: полотно в плоскости стены (узел — на листе узлов)
- стены и перекрытия в сечении
- окраска: тон — цвет по коду производителя (условно)
- О1 — марка отделки по реестру отделки альбома
- А — марка развёртки: буква стены, стрелка взгляд

Ведомость отделки (на листе)

Марка	Поверхность	Материал, изделие	Цвет, код	Кол.
О1	стены	окраска, Farrow & Ball Modern Emulsion, матовая, подготовка Q3	Farrow & Ball No. 241 «Skimming Stone»	6,1 м²
О3	плинтус	плинтус МДФ, h 80 мм, аналог: плинтус МДФ под покраску 80×16	Farrow & Ball No. 241 «Skimming Stone»	0,4 м
О4	потолок	окраска, Tikkurila Anti-Reflex 2, глубокоматовая, подготовка Q3	Tikkurila V503 «Winter»	17,8 м²

Схема развёрток (М 1:100)

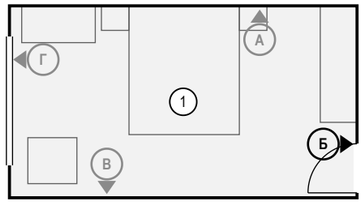

Ведомость изделий и проёмов (на листе)

Марка	Изделие, проём	На виде Ш×В, мм	Низ, мм
С5	шкаф распашной	1885×2400	0
Д-2	дверь скрытого монтажа	800×2100	0

Примечания

1. Развёртки — вид на стену изнутри помещения, по часовой стрелке; расположение — на схеме листа и на листе 89; размеры — в мм по чистовым поверхностям; отметки — в м от ±0,000; высоты Н — от чистого пола помещения до оси изделия, у декора — до центра.
2. Красная цепочка — привязки электроточек и выводов по осям от угла чистовых стен; высота Н — у знака, от чистого пола до оси; высоты мебели, проёмов и границ отделки — колонкой отметок слева. У знака — короткая марка; назначение, группа щита, высота и привязка каждой точки и вывода — в «Ведомости точек и выводов» под видами (каждая точка — строка).
3. У знака электроточки: марка (Р — розетка, S — выключатель, Св — светильник, ЭВ — вывод кабеля), ×N — число постов в рамке, гр. — группа щита, Н — высота оси от чистого пола, мм; группы по клавишам выключателя — на листе выключателей.
4. Схема мебели, приборов и декора не является технической документацией для производства мебели; габариты — по паспортам изделий.
5. Двери скрытого монтажа — полотно в плоскости стены, отделка стены по полотну, плинтус прерывается у короба (узел — на листе узлов).
6. Потолок — у каждой стены свой, по плану потолков (ПТ1); ступени — зоной, кромка короба перед нишей — тонкой линией; в поле потолка: ПТ2 +2,600.

Допущения и предложения на листе. Основа листа: размеры сняты со скана плана заказчика по размерным цепочкам, контрольный обмер на объекте не выполнялся (К-13); высота потолка 2700 мм принята: на плане заказчика не указана (К-11); толщины стен приняты: наружные 250 мм, перегородки 150 мм (на плане 85–190 мм) (К-13); разрешённая мощность 15 кВт принята по типовой квартире, технических условий нет (К-14); утолщение стены 190 × 1360 мм и элемент 1470 × 160 мм плана заказчика не определены (К-12); ниши санузла 2 закрыты перегородкой и фальш-стеной: проектное решение, на плане заказчика ниша у входа открыта (К-18); несущие стены не определены: до технического заключения все существующие стены считаются несущими (К-20); окна существующие и сохраняются; подоконная доска и глубина откосов не заданы — приняты, не замерены (К-27); подрайон климата не задан — принят не северный (жилые от 2,5 м) (К-29). Знак «*» — принято, не замерено (замерить): К-13: отметка существующего пола. См. лист открытых вопросов (лист 7, записи К-11–К-14, К-18, К-20; лист 8, записи К-27, К-29).

1000 мм · печать 1:1

Изм.	Кол.уч	Лист	№ док.	Подп.	Дата
Разраб.		Кырлан А.С.			13.11.26
Пров.					
ГИП					
Н. контр.					
Утв.					

ГД-2026-003-АИ

Трёхкомнатная квартира

Общая площадь 78,95* м² · * размеры со скана, не замерены (реестр — л. 6–11, К-13)

Дизайн-проект интерьера трёхкомнатной квартиры

Стадия	Лист	Листов
РП	91	132

Развёртка стены Б. Спальня 1 (пом. 1)

М 1:20

Кырлан Александр Сергеевич


выпуск 13.11.2026 № 6f3a8abb2c · стр. 100 из 157

Развёртка стены В. Спальня 1 (пом. 1)

Спальня 1 (пом. 1) · вид изнутри помещения · размеры в мм, отметки в м

ПРЕДВАРИТЕЛЬНО · не для производства работ · открыто пунктов: 28 (реестр — л. 6–11)

Стена В (М 1:25)

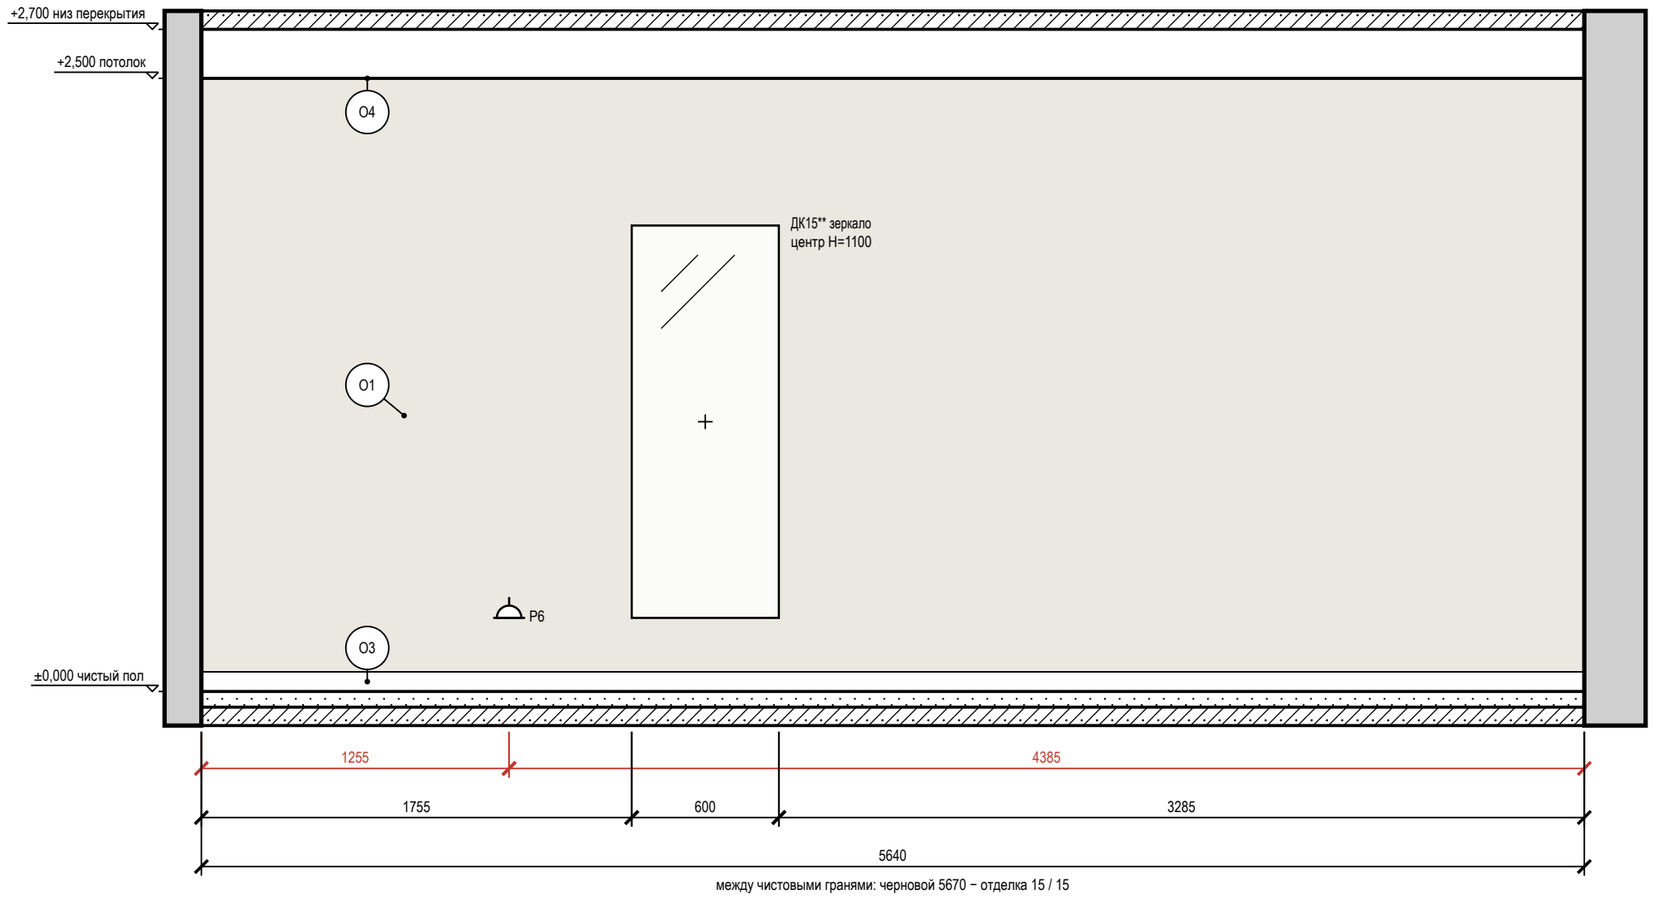


между чистовыми гранями: черновой 5670 − отделка 15 / 15

Условные обозначения

- розетка с заземляющим контактом; у знака — марка, ×N постов в рамке, гр. — группа щита, Н — высота оси, мм
- привязки точек и выводов от угла и от пола, мм
- мебель и приборы — фасад по расстановке (условно)
- зеркало: марка Д, крест — центр, Н — высота центра, мм
- стены и перекрытия в сечении
- окраска: тон — цвет по коду производителя (условно)
- О1 — марка отделки по реестру отделки альбома
- А — марка развёртки: буква стены, стрелка — взгляд

Схема развёрток (М 1:100)

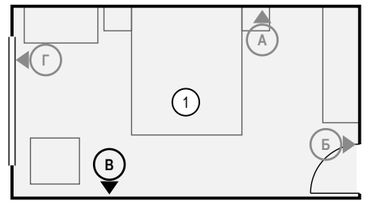

Ведомость точек и выводов

Марка	Что это	Гр.	Н, мм	От угла, мм	Примечание
Р6	розетка: уборка	4	300	1255	

Ведомость изделий и проёмов (на листе)

Марка	Изделие, проём	На виде Ш×В, мм	Низ, мм
ДК15**	зеркало	600×1600	300

Примечания

1. Развёртки — вид на стену изнутри помещения, по часовой стрелке; расположение — на схеме листа и на листе 89; размеры — в мм по чистовым поверхностям; отметки — в м от ±0,000; высоты Н — от чистого пола помещения до оси изделия, у декора — до центра.
2. Красная цепочка — привязки электроточек и выводов по осям от угла чистовых стен; высота Н — у знака, от чистого пола до оси; высоты мебели, проёмов и границ отделки — колонкой отметок слева. У знака — короткая марка; назначение, группа щита, высота и привязка каждой точки и вывода — в «Ведомости точек и выводов» под видами (каждая точка — строка).
3. Отделка стен — по ведомости отделки помещений, лист 67.
4. У знака электроточки: марка (Р — розетка, S — выключатель, Св — светильник, ЭВ — вывод кабеля), ×N — число постов в рамке, гр. — группа щита, Н — высота оси от чистого пола, мм; группы по клавишам выключателя — на листе выключателей.
5. Схема мебели, приборов и декора не является технической документацией для производства мебели; габариты — по паспортам изделий.
6. Картины и зеркала крепить к основанию по паспорту изделия (закладные и анкеры — в перечне скрытых работ); крест — ось центра предмета.
7. Потолок — у каждой стены свой, по плану потолков (ПТ1); ступени — зоной, кромка короба перед нишей — тонкой линией; в поле потолка: ПТ2 +2,600.

Допущения и предложения на листе

Основа листа: размеры сняты со скана плана заказчика по размерным цепочкам, контрольный обмер на объекте не выполнялся (К-13); высота потолка 2700 мм принята: на плане заказчика не указана (К-11); толщины стен приняты: наружные 250 мм, перегородки 150 мм (на плане 85–190 мм) (К-13); разрешённая мощность 15 кВт принята по типовой квартире, технических условий нет (К-14); утолщение стены 190 × 1360 мм и элемент 1470 × 160 мм плана заказчика не определены (К-12); ниши санузла 2 закрыты перегородкой и фальш-стеной: проектное решение, на плане заказчика ниша у входа открыта (К-18); несущие стены не определены: до технического заключения все существующие стены считаются несущими (К-20); окна существующие и сохраняются; подоконная доска и глубина откосов не заданы — приняты, не замерены (К-27); подрайон климата не задан — принят не северный (жилые от 2,5 м) (К-29).

Знак «*» — принято, не замерено и не подтверждено (замерить на объекте): К-13: отметка существующего пола — отметка существующего пола и верха плиты не замерена: на плане заказчика отметок нет; нивелировка — в задании на обмер (К-13).

Знак «**» — предложение проектировщика, заказчиком не утверждено (согласовать с заказчиком): ИЗ-20: ДК15.

См. лист открытых вопросов (лист 7, записи К-11–К-14, К-18, К-20; лист 8, записи К-27, К-29; лист 11, запись ИЗ-20).

1000 мм · печать 1:1

Изм.	Кол.уч	Лист	№ док.	Подп.	Дата
Разраб.		Кырлан А.С.			13.11.26
Пров.					
ГИП					
Н. контр.					
Утв.					

ГД-2026-003-АИ

Трёхкомнатная квартира

Общая площадь 78,95* м² · * размеры со скана, не замерены (реестр — л. 6–11, К-13)

Дизайн-проект интерьера трёхкомнатной квартиры

Стадия	Лист	Листов
РП	92	132

Развёртка стены В. Спальня 1 (пом. 1)

М 1:25

Кырлан Александр Сергеевич


выпуск 13.11.2026 № 6f3a8abb2c · стр. 101 из 157

Развёртка стены Г. Спальня 1 (пом. 1)

Спальня 1 (пом. 1) · вид изнутри помещения · размеры в мм, отметки в м

ПРЕДВАРИТЕЛЬНО · не для производства работ · открыто пунктов: 28 (реестр — л. 6–11)

Стена Г (М 1:20)

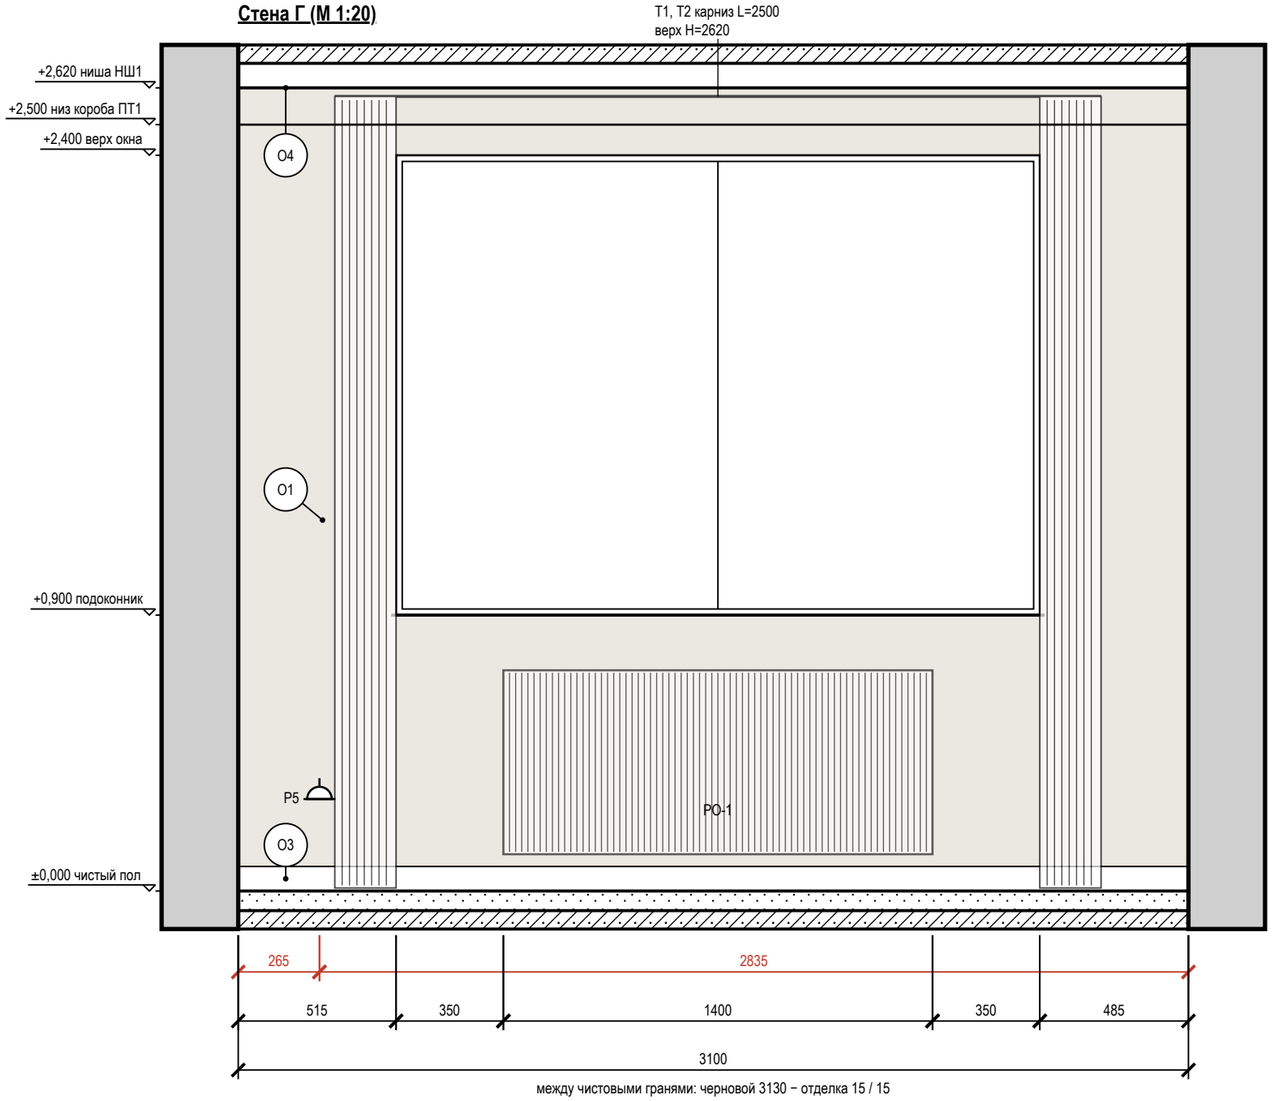

между чистовыми гранями: черновой 3130 − отделка 15 / 15

Ведомость точек и выводов

Марка	Что это	Гр.	H, мм	От угла, мм	Примечание
Р5	розетка: торшер у кресла	4	300	265	


Условные обозначения

- розетка с заземляющим контактом; у знака марка, ×N — постов в рамке, гр. — группа щита, H — высота оси, мм
- привязки точек и выводов от угла и от пола, мм
- мебель и приборы — фасад по расстановке (условно)
- карниз (шина) и шторы в собранном виде: марка Т, длина L, верх H
- окно: проём, рама, подоконник
- радиатор отопления; марка — по плану отопления
- стены и перекрытия в сечении
- окраска: тон — цвет по коду производителя (условно)
- О1 — марка отделки по реестру отделки альбома
- A — марка развёртки: буква стены, стрелка взгляд

Ведомость отделки (на листе)

Марка	Поверхность	Материал, изделие	Цвет, код	Кол.
О1	стены	окраска, Farrow & Ball Modern Emulsion, матовая, подготовка Q3	Farrow & Ball No. 241 «Skimming Stone»	5 м²
О3	плинтус	плинтус МДФ, h 80 мм, аналог: плинтус МДФ под покраску 80×16	Farrow & Ball No. 241 «Skimming Stone»	3,1 м
О4	потолок	окраска, Tikkurila Anti-Reflex 2, глубокоматовая, подготовка Q3	Tikkurila V503 «Winter»	17,8 м²

Схема развёрток (М 1:100)

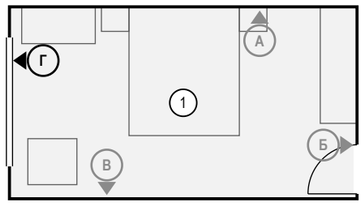

Ведомость изделий и проёмов (на листе)

Марка	Изделие, проём	На виде Ш×В, мм	Низ, мм
РО-1	радиатор отопления	1400×600	120

Примечания

1. Развёртки — вид на стену изнутри помещения, по часовой стрелке; расположение — на схеме листа и на листе 89; размеры — в мм по чистовым поверхностям; отметки — в м от ±0,000; высоты H — от чистого пола помещения до оси изделия, у декора — до центра.
2. Красная цепочка — привязки электроточек и выводов по осям от угла чистовых стен; высота H — у знака, от чистого пола до оси; высоты мебели, проёмов и границ отделки — колонкой отметок слева. У знака — короткая марка; назначение, группа щита, высота и привязка каждой точки и вывода — в «Ведомости точек и выводов» под видами (каждая точка — строка).
3. У знака электроточки: марка (Р — розетка, S — выключатель, Св — светильник, ЭВ — вывод кабеля), ×N — число постов в рамке, гр. — группа щита, H — высота оси от чистого пола, мм; группы по клавишам выключателя — на листе выключателей.
4. Схема мебели, приборов и декора не является технической документацией для производства мебели; габариты — по паспортам изделий.
5. Карнизы (шины) — по ведомости текстиля декоратора: длина L и верх H на развёртке — те же числа, что в ведомости; крепление — до окраски потолка.
6. Потолок — у каждой стены свой, по плану потолков (НШ1, ПТ1); ступени — зоной, кромка короба перед нишей — тонкой линией; в поле потолка: ПТ2 +2,600.

Допущения и предложения на листе. Основа листа: размеры сняты со скана плана заказчика по размерным цепочкам, контрольный обмер на объекте не выполнялся (К-13); высота потолка 2700 мм принята: на плане заказчика не указана (К-11); толщины стен приняты: наружные 250 мм, перегородки 150 мм (на плане 85–190 мм) (К-13); разрешённая мощность 15 кВт принята по типовой квартире, технических условий нет (К-14); утолщение стены 190 × 1360 мм и элемент 1470 × 160 мм плана заказчика не определены (К-12); ниши санузла 2 закрыты перегородкой и фальш-стеной: проектное решение, на плане заказчика ниша у входа открыта (К-18); несущие стены не определены: до технического заключения все существующие стены считаются несущими (К-20); окна существующие и сохраняются; подоконная доска и глубина откосов не заданы — приняты, не замерены (К-27); подрайон климата не задан — принят не северный (жилые от 2,5 м) (К-29). Знак «*» — принято, не замерено (замерить): К-13: отметка существующего пола. См. лист открытых вопросов (лист 7, записи К-11–К-14, К-18, К-20; лист 8, записи К-27, К-29).

1000 мм · печать 1:1

Изм.	Кол.уч	Лист	№ док.	Подп.	Дата
Разраб.		Кырлан А.С.			13.11.26
Пров.					
ГИП					
Н. контр.					
Утв.					

ГД-2026-003-АИ

Трёхкомнатная квартира

Общая площадь 78,95* м² · * размеры со скана, не замерены (реестр — л. 6–11, К-13)

Дизайн-проект интерьера трёхкомнатной квартиры

Стадия	Лист	Листов
РП	93	132

Развёртка стены Г. Спальня 1 (пом. 1)

М 1:20

Кырлан Александр Сергеевич


выпуск 13.11.2026 № 6f3a8abb2c · стр. 102 из 157

Развёртки стен А, Б. Ванная (пом. 2)

Ванная (пом. 2) · вид изнутри помещения · размеры в мм, отметки в м


ПРЕДВАРИТЕЛЬНО · не для производства работ · открыто пунктов: 28 (реестр — л. 6–11)

Стена А (М 1:25)

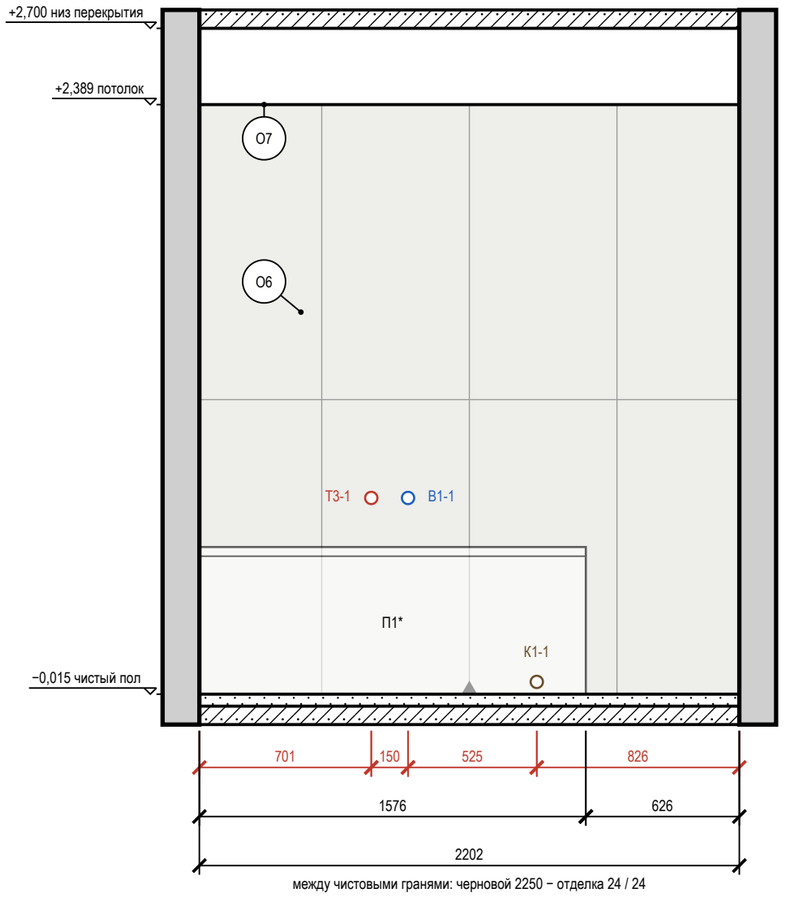

между чистовыми гранями: черновой 2250 − отделка 24 / 24

Стена Б (М 1:25)

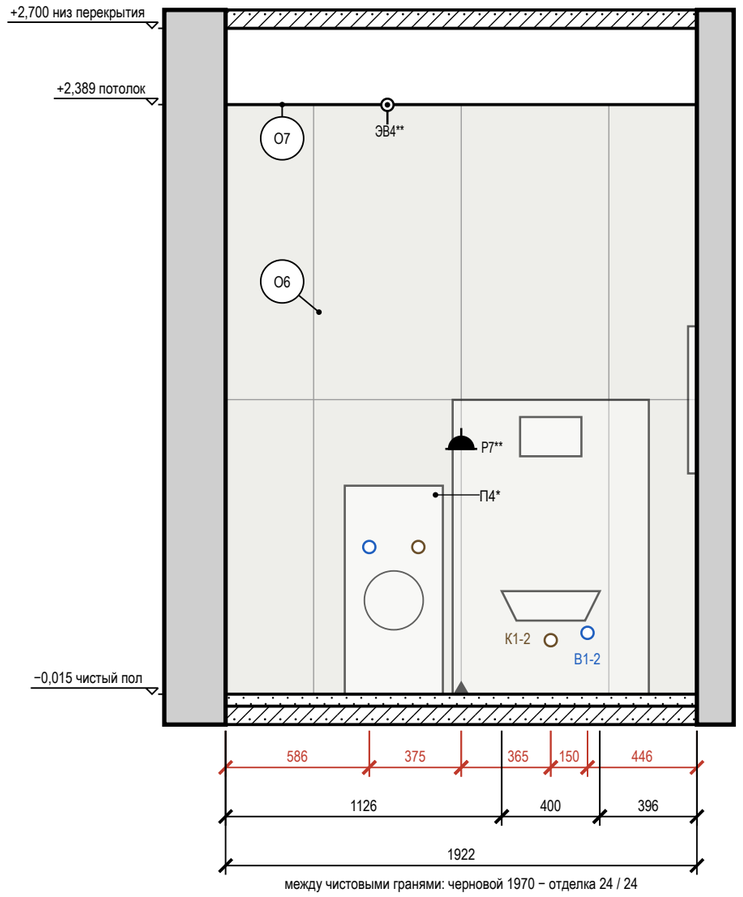


между чистовыми гранями: черновой 1970 − отделка 24 / 24

Условные обозначения

- розетка влагозащищённая IP44
- вывод кабеля для подключения прибора (без розетки), марка ЭВ
- вывод В1 (код — в ведомости привязок)
- вывод Т3 (код — в ведомости привязок)
- вывод К1 (код — в ведомости привязок)
- привязки точек и выводов от угла и от пола, мм
- мебель и приборы — фасад по расстановке (условно)
- стены и перекрытия в сечении
- плитка: сетка швов по формату, ▲ — ось старта
- О1 — марка отделки по реестру отделки альбома
- А — марка развёртки: буква стены, стрелка — взгляд

Схема развёрток (М 1:50)

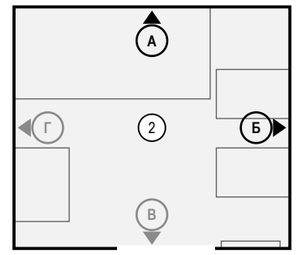

Ведомость точек и выводов

Стена	Марка	Что это	Гр.	Н, мм	От угла, мм	Примечание
А	Т3-1	горячая вода — ванна		800*	701	межос. 150
А	В1-1	холодная вода — ванна		800*	851	межос. 150
А	К1-1	канализация — ванна		50*	1376	Ø50
Б	В1-4	холодная вода — стиральная машина		600*	586	кран машины
Б	ЭВ4**	вывод кабеля: вентилятор ВР1 (таймер выбега)	3	2403	660	

Стена	Марка	Что это	Гр.	Н, мм	От угла, мм	Примечание
Б	К1-4	канализация — стиральная машина		600*	786	Ø50
Б	Р7**	розетка: стиральная машина	12	1000	961	IP44
Б	К1-2	канализация — унитаз подвесной		220*	1326	Ø110
Б	В1-2	холодная вода — унитаз подвесной		250*	1476	в раме инсталляции

Ведомость отделки (на листе)

Марка	Поверхность	Материал, изделие	Цвет, код	Кол.
О6	стены	облицовка плиткой, 600×1200×9 мм, аналог: керамогранит под травертин, матовый, затирка CG2WA		9,9 м²
О7	потолок	окраска, Tikkurila Luja 7, матовая, подготовка Q3	Tikkurila V503 «Winter»	4,4 м²

Примечания

1. Развёртки — вид на стену изнутри помещения, по часовой стрелке; расположение — на схеме листа и на листе 89; размеры — в мм по чистовым поверхностям; отметки — в м от ±0,000; высоты Н — от чистого пола помещения до оси изделия, у декора — до центра.
2. Красная цепочка — привязки электроточек и выводов по осям от угла чистовых стен; высота Н — у знака, от чистого пола до оси; высоты мебели, проёмов и границ отделки — колонкой отметок слева. У знака — короткая марка; назначение, группа щита, высота и привязка каждой точки и вывода — в «Ведомости точек и выводов» под видами (каждая точка — строка).
3. У знака электроточки: марка (Р — розетка, S — выключатель, Св — светильник, ЭВ — вывод кабеля), ×N — число постов в рамке, гр. — группа щита, Н — высота оси от чистого пола, мм; группы по клавишам выключателя — на листе выключателей.
4. Схема мебели, приборов и декора не является технической документацией для производства мебели; габариты — по паспортам изделий (* — высота не задана в проекте, показана по типовому изделию).
5. Выводы ВК — коды и высоты по листу выводов сантехники; * — высота принята по типовой практике монтажа, окончательно — по паспорту прибора.
6. Облицовка — по сетке швов 2 мм, раскладка от оси стены (треугольник у пола), целые ряды от пола; подрезки — по листу раскладки плитки.
7. Гидроизоляция в 2 слоя, заход на стены 200 мм; над ванной — до 2000 и 300 мм за борт — до облицовки, с актом скрытых работ и тестом проливом (узел — на листе узлов).
8. Часть марок не уместилась у знаков: коды, высоты и привязки этих позиций — в ведомости точек и выводов под видами.

1000 мм · печать 1:1

Допущения и предложения на листе. Знак «*» принято (замерить): отметка существующего пола. Знак «**» предложено (согласовать). См. лист открытых вопросов (листы 6–11).

Изм.	Кол.уч	Лист	№ док.	Подп.	Дата
Разраб.		Кырлан А.С.			13.11.26
Пров.					
ГИП					
Н. контр.					
Утв.					

ГД-2026-003-АИ

Трёхкомнатная квартира

Общая площадь 78,95* м² · * размеры со скана, не замерены (реестр — л. 6–11, К-13)

Дизайн-проект интерьера трёхкомнатной квартиры

Стадия	Лист	Листов
РП	94	132

Развёртки стен А, Б. Ванная (пом. 2)

М 1:25

Кырлан Александр Сергеевич


выпуск 13.11.2026 № 6f3a8abb2c · стр. 103 из 157

Развёртки стен В, Г. Ванная (пом. 2)

Ванная (пом. 2) · вид изнутри помещения · размеры в мм, отметки в м


ПРЕДВАРИТЕЛЬНО · не для производства работ · открыто пунктов: 28 (реестр — л. 6–11)

Стена В (М 1:25)

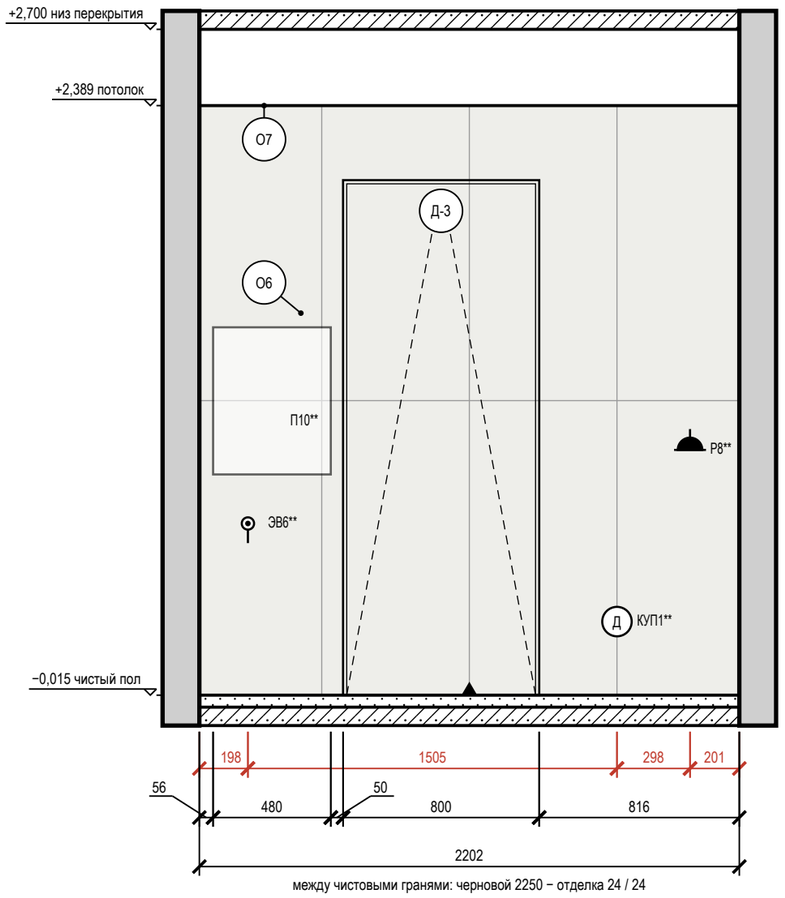

между чистовыми гранями: черновой 2250 − отделка 24 / 24

Стена Г (М 1:25)

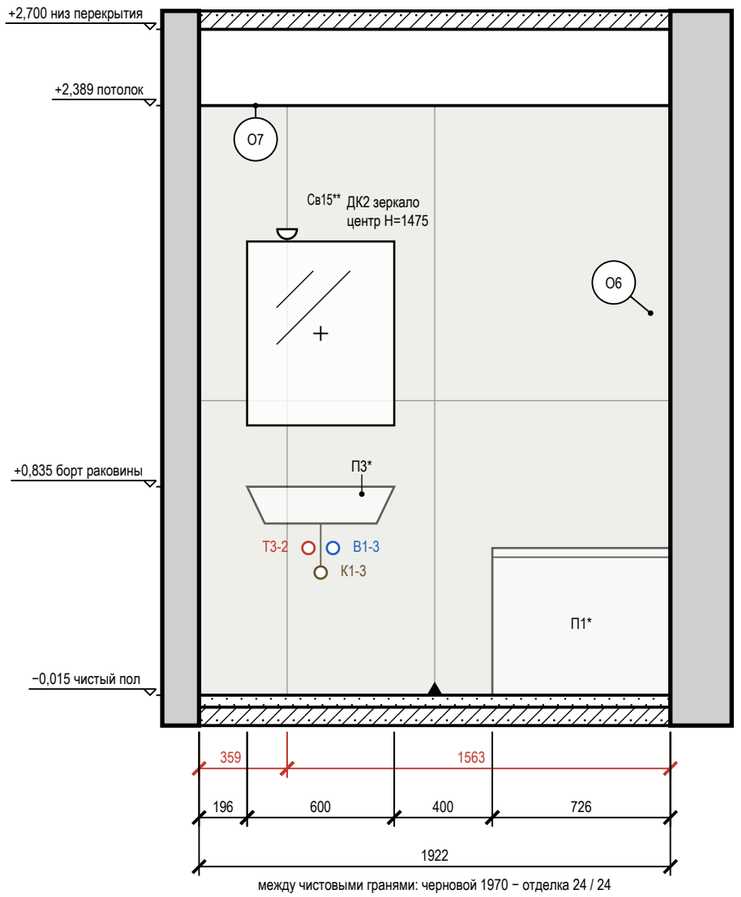

между чистовыми гранями: черновой 1970 − отделка 24 / 24

Условные обозначения

- розетка влагозащищённая IP44
- вывод кабеля для подключения прибора (без розетки), марка ЭВ
- светильник настенный (бра), Н — высота оси
- вывод В1 (код — в ведомости привязок)
- вывод Т3 (код — в ведомости привязок)
- вывод К1 (код — в ведомости привязок)
- привязки точек и выводов от угла и от пола, мм
- мебель и приборы — фасад по расстановке (условно)
- зеркало: марка Д, крест — центр, Н — высота центра, мм
- дверь скрытого монтажа: полотно в плоскости стены (узел — на листе узлов)
- стены и перекрытия в сечении
- плитка: сетка швов по формату, ▲ — ось старта
- О1 — марка отделки по реестру отделки альбома
- А — марка развёртки: буква стены, стрелка — взгляд

Ведомость отделки (на листе)


Марка	Поверхность	Материал, изделие	Цвет, код	Кол.
О6	стены	облицовка плиткой, 600×1200×9 мм, аналог: керамогранит под травертин, матовый, затирка CG2WA		8,2 м²
О7	потолок	окраска, Tikkurila Luja 7, матовая, подготовка Q3	Tikkurila V503 «Winter»	4,4 м²

Ведомость точек и выводов

Стена	Марка	Что это	Гр.	Н, мм	От угла, мм	Примечание
В	ЭВ6**	вывод кабеля: полотенцесушитель П10**	13	700	198	
В	КУП1**	КУП (уравнивание потенциалов): КУП уравнивание потенциалов (ДСУП)		300	1703	
В	Р8**	розетка: фен у умывальника	13	1000	2001	IP44
Г	Св15**	светильник настенный	3	1900	359	

Стена	Марка	Что это	Гр.	Н, мм	От угла, мм	Примечание
Г	Т3-2	горячая вода — умывальник		600*	446	межос. 100
Г	К1-3	канализация — умывальник		500*	496	Ø50
Г	В1-3	холодная вода — умывальник		600*	546	межос. 100

Схема развёрток (М 1:50)

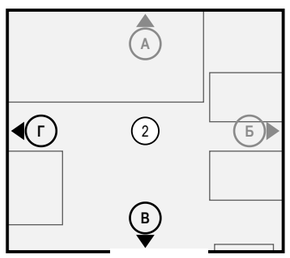

Примечания

1. Развёртки — вид на стену изнутри помещения, по часовой стрелке; расположение — на схеме листа и на листе 89; размеры — в мм по чистовым поверхностям; отметки — в м от ±0,000; высоты Н — от чистого пола помещения до оси изделия, у декора — до центра.
2. Красная цепочка — привязки электроточек и выводов по осям от угла чистовых стен; высота Н — у знака, от чистого пола до оси; высоты мебели, проёмов и границ отделки — колонкой отметок слева. У знака — короткая марка; назначение, группа щита, высота и привязка каждой точки и вывода — в «Ведомости точек и выводов» под видами (каждая точка — строка).
3. У знака электроточки: марка (Р — розетка, S — выключатель, Св — светильник, ЭВ — вывод кабеля), ×N — число постов в рамке, гр. — группа щита, Н — высота оси от чистого пола, мм; группы по клавишам выключателя — на листе выключателей.
4. Схема мебели, приборов и декора не является технической документацией для производства мебели; габариты — по паспортам изделий (* — высота не задана в проекте, показана по типовому изделию).
5. Выводы ВК — коды и высоты по листу выводов сантехники; * — высота принята по типовой практике монтажа, окончательно — по паспорту прибора.
6. Облицовка — по сетке швов 2 мм, раскладка от оси стены (треугольник у пола), целые ряды от пола; подрезки — по листу раскладки плитки.
7. Гидроизоляция в 2 слоя, заход на стены 200 мм; над ванной — до 2000 и 300 мм за борт — до облицовки, с актом скрытых работ и тестом проливом (узел — на листе узлов).
8. Картины и зеркала крепить к основанию по паспорту изделия (закладные и анкеры — в перечне скрытых работ); крест — ось центра предмета.
9. Двери скрытого монтажа — полотно в плоскости стены, отделка стены по полотну, плинтус прерывается у короба (узел — на листе узлов).

Допущения и предложения на листе. Знак «*» принято (замерить): отметка существующего пола. Знак «**» предложено (согласовать). См. лист открытых вопросов (листы 6–11).

1000 мм · печать 1:1

Изм.	Кол.уч	Лист	№ док.	Подп.	Дата
Разраб.		Кырлан А.С.			13.11.26
Пров.					
ГИП					
Н. контр.					
Утв.					

ГД-2026-003-АИ

Трёхкомнатная квартира

Общая площадь 78,95* м² · * размеры со скана, не замерены (реестр — л. 6–11, К-13)

Дизайн-проект интерьера трёхкомнатной квартиры

Стадия	Лист	Листов
РП	95	132

Развёртки стен В, Г. Ванная (пом. 2)

М 1:25

Кырлан Александр Сергеевич


выпуск 13.11.2026 № 6f3a3abb2c · стр. 104 из 157

Развёртки стен А, Б. Гардеробная (пом. 3)

Гардеробная (пом. 3) · вид изнутри помещения · размеры в мм, отметки в м


ПРЕДВАРИТЕЛЬНО · не для производства работ · открыто пунктов: 28 (реестр — л. 6–11)

Стена А (М 1:20)

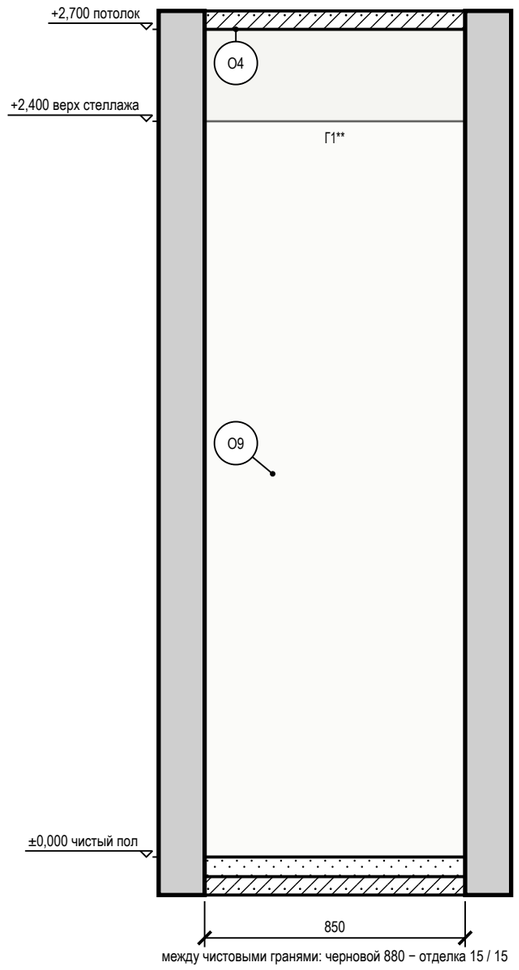

между чистовыми гранями: черновой 880 − отделка 15 / 15

Стена Б (М 1:20)

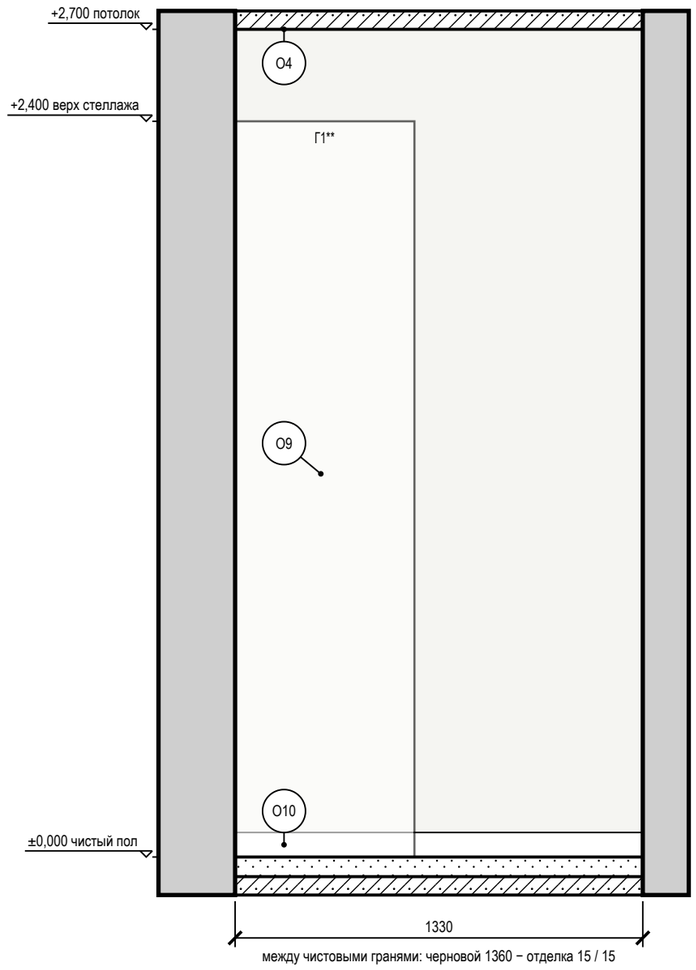


между чистовыми гранями: черновой 1360 − отделка 15 / 15

Ведомость отделки (на листе)

Марка	Поверхность	Материал, изделие	Цвет, код	Кол.
О4	потолок	окраска, Tikkurila Anti-Reflex 2, глубокоматовая, подготовка Q3	Tikkurila V503 «Winter»	1,9 м²
О9	стены	окраска, Tikkurila Harmony, матовая, подготовка Q3	Tikkurila V503 «Winter»	5,9 м²
О10	плинтус	плинтус МДФ, h 80 мм, аналог: плинтус МДФ под покраску 80×16	Tikkurila V503 «Winter»	1,3 м

Схема развёрток (М 1:50)

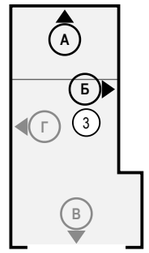

Допущения и предложения на листе

Основа листа: размеры сняты со скана плана заказчика по размерным цепочкам, контрольный обмер на объекте не выполнялся (К-13); высота потолка 2700 мм принята: на плане заказчика не указана (К-11); толщины стен приняты: наружные 250 мм, перегородки 150 мм (на плане 85–190 мм) (К-13); разрешённая мощность 15 кВт принята по типовой квартире, технических условий нет (К-14); утолщение стены 190 × 1360 мм и элемент 1470 × 160 мм плана заказчика не определены (К-12); ниши санузла 2 закрыты перегородкой и фальш-стеной: проектное решение, на плане заказчика ниша у входа открыта (К-18); несущие стены не определены: до технического заключения все существующие стены считаются несущими (К-20); окна существующие и сохраняются; подоконная доска и глубина откосов не заданы — приняты, не замерены (К-27); подрайон климата не задан — принят не северный (жилые от 2,5 м) (К-29).

Знак «*» — принято, не замерено и не подтверждено (замерить на объекте): К-13: отметка существующего пола — отметка существующего пола и верха плиты не замерена: на плане заказчика отметок нет; нивелировка — в задании на обмер (К-13).

Знак «**» — предложение проектировщика, заказчиком не утверждено (согласовать с заказчиком): К-9: Г1 — гардеробная 880 мм: система глубиной 600 вдоль длинной стены оставляла проход 280 мм — система перенесена на торцевую стену А, проход по всей ширине 880 мм.

См. лист открытых вопросов (лист 6, запись К-9; лист 7, записи К-11–К-14, К-18, К-20; лист 8, записи К-27, К-29).

Условные обозначения

- мебель и приборы — фасад по расстановке (условно)
- стены и перекрытия в сечении
- окраска: тон — цвет по коду производителя (условно)
- О1 — марка отделки по реестру отделки альбома
- А — марка развёртки: буква стены, стрелка — взгляд

Ведомость изделий и проёмов (на листе)

Стена	Марка	Изделие, проём	На виде Ш×В, мм	Низ, мм
А	Г1**	система хранения у торцевой стены: штанга вдоль стены, полки, ящики	850×2400	0
Б	Г1**	система хранения у торцевой стены: штанга вдоль стены, полки, ящики	585×2400	0

Примечания

1. Развёртки — вид на стену изнутри помещения, по часовой стрелке; расположение — на схеме листа и на листе 89; размеры — в мм по чистовым поверхностям; отметки — в м от ±0,000; высоты Н — от чистого пола помещения до оси изделия, у декора — до центра.
2. Схема мебели, приборов и декора не является технической документацией для производства мебели; габариты — по паспортам изделий.

1000 мм · печать 1:1

Изм.	Кол.уч	Лист	№ док.	Подп.	Дата
Разраб.		Кырлан А.С.			13.11.26
Пров.					
ГИП					
Н. контр.					
Утв.					

ГД-2026-003-АИ

Трёхкомнатная квартира

Общая площадь 78,95* м² · * размеры со скана, не замерены (реестр — л. 6–11, К-13)

Дизайн-проект интерьера трёхкомнатной квартиры	Стадия	Лист	Листов
	РП	96	132
Развёртки стен А, Б. Гардеробная (пом. 3) М 1:20	**Кырлан Александр Сергеевич**		


выпуск 13.11.2026 № 6f3a8abb2c · стр. 105 из 157

Развёртки стен В, Г. Гардеробная (пом. 3)

Гардеробная (пом. 3) · вид изнутри помещения · размеры в мм, отметки в м


ПРЕДВАРИТЕЛЬНО · не для производства работ · открыто пунктов: 28 (реестр — л. 6–11)

Стена В (М 1:20)

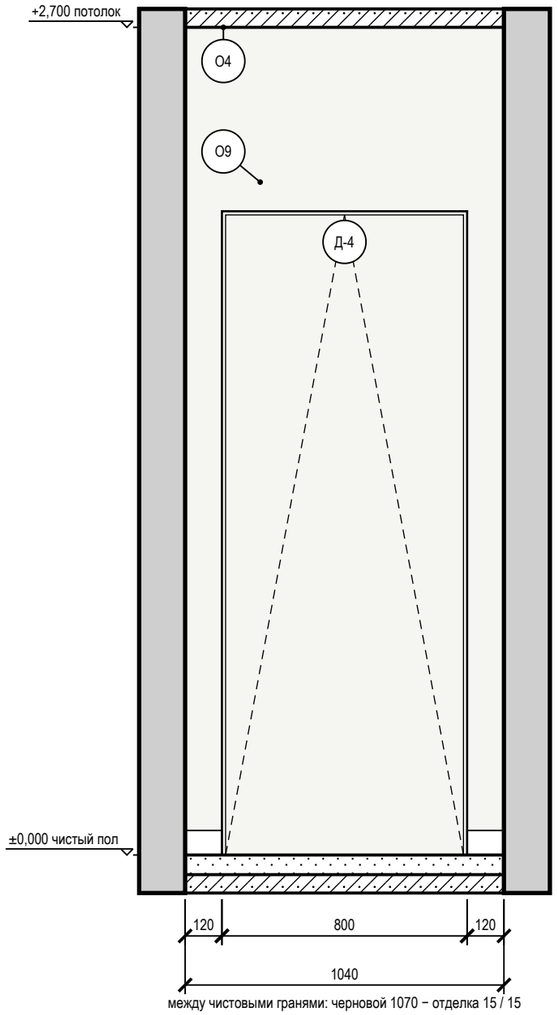

между чистовыми гранями: черновой 1070 − отделка 15 / 15

Стена Г (М 1:20)

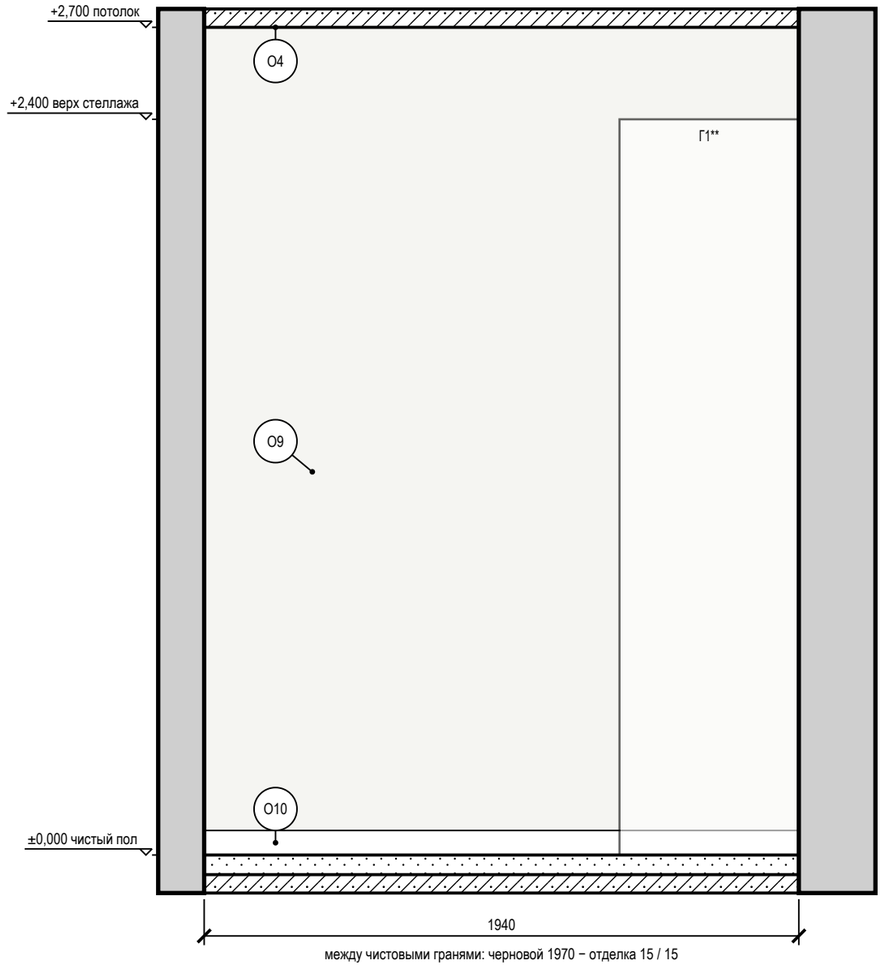

между чистовыми гранями: черновой 1970 − отделка 15 / 15


Условные обозначения

- мебель и приборы — фасад по расстановке (условно)
- дверь скрытого монтажа: полотно в плоскости стены (узел — на листе узлов)
- стены и перекрытия в сечении
- окраска: тон — цвет по коду производителя (условно)
- О1 — марка отделки по реестру отделки альбома
- A — марка развёртки: буква стены, стрелка — взгляд

Ведомость отделки (на листе)

Марка	Поверхность	Материал, изделие	Цвет, код	Кол.
О4	потолок	окраска, Tikkurila Anti-Reflex 2, глубокоматовая, подготовка Q3	Tikkurila V503 «Winter»	1,9 м²
О9	стены	окраска, Tikkurila Harmony, матовая, подготовка Q3	Tikkurila V503 «Winter»	6,4 м²
О10	плинтус	плинтус МДФ, h 80 мм, аналог: плинтус МДФ под покраску 80×16	Tikkurila V503 «Winter»	2,2 м

Схема развёрток (М 1:50)

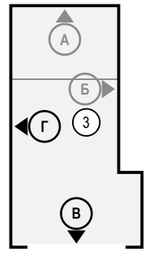

Ведомость изделий и проёмов (на листе)

Стена	Марка	Изделие, проём	На виде Ш×В, мм	Низ, мм
В	Д-4	дверь скрытого монтажа	800×2100	0
Г	Г1**	система хранения у торцевой стены: штанга вдоль стены, полки, ящики	585×2400	0

Примечания

1. Развёртки — вид на стену изнутри помещения, по часовой стрелке; расположение — на схеме листа и на листе 89; размеры — в мм по чистовым поверхностям; отметки — в м от ±0,000; высоты Н — от чистого пола помещения до оси изделия, у декора — до центра.
2. Схема мебели, приборов и декора не является технической документацией для производства мебели; габариты — по паспортам изделий.
3. Двери скрытого монтажа — полотно в плоскости стены, отделка стены по полотну, плинтус прерывается у короба (узел — на листе узлов).

Допущения и предложения на листе. Основа листа: размеры сняты со скана плана заказчика по размерным цепочкам, контрольный обмер на объекте не выполнялся (К-13); высота потолка 2700 мм принята: на плане заказчика не указана (К-11); толщины стен приняты: наружные 250 мм, перегородки 150 мм (на плане 85–190 мм) (К-13); разрешённая мощность 15 кВт принята по типовой квартире, технических условий нет (К-14); утолщение стены 190 × 1360 мм и элемент 1470 × 160 мм плана заказчика не определены (К-12); ниши санузла 2 закрыты перегородкой и фальш-стеной: проектное решение, на плане заказчика ниша у входа открыта (К-18); несущие стены не определены: до технического заключения все существующие стены считаются несущими (К-20); окна существующие и сохраняются; подоконная доска и глубина откосов не заданы — приняты, не замерены (К-27); подрайон климата не задан — принят не северный (жилые от 2,5 м) (К-29). Знак «*» — принято, не замерено и не подтверждено (замерить на объекте): К-13: отметка существующего пола — отметка существующего пола и верха плиты не замерена: на плане заказчика отметок нет; нивелировка — в задании на обмер (К-13). Знак «**» — предложение проектировщика, заказчиком не утверждено (согласовать с заказчиком): К-9: Г1 — гардеробная 880 мм: система глубиной 600 вдоль длинной стены оставляла проход 280 мм — система перенесена на торцевую стену А, проход по всей ширине 880 мм. См. лист открытых вопросов (лист 6, запись К-9; лист 7, записи К-11–К-14, К-18, К-20; лист 8, записи К-27, К-29).

1000 мм · печать 1:1

Изм.	Кол.уч	Лист	№ док.	Подп.	Дата
Разраб.		Кырлан А.С.			13.11.26
Пров.					
ГИП					
Н. контр.					
Утв.					

ГД-2026-003-АИ

Трёхкомнатная квартира

Общая площадь 78,95* м² · * размеры со скана, не замерены (реестр — л. 6–11, К-13)

Дизайн-проект интерьера трёхкомнатной квартиры

Стадия	Лист	Листов
РП	97	132

Развёртки стен В, Г. Гардеробная (пом. 3)

М 1:20

Кырлан Александр Сергеевич


выпуск 13.11.2026 · 6f3a8abb2c · стр. 106 из 157

Развёртка стены А. Спальня 2 (пом. 4)

Спальня 2 (пом. 4) · вид изнутри помещения · размеры в мм, отметки в м

ПРЕДВАРИТЕЛЬНО · не для производства работ · открыто пунктов: 28 (реестр — л. 6–11)

Стена А (М 1:20)

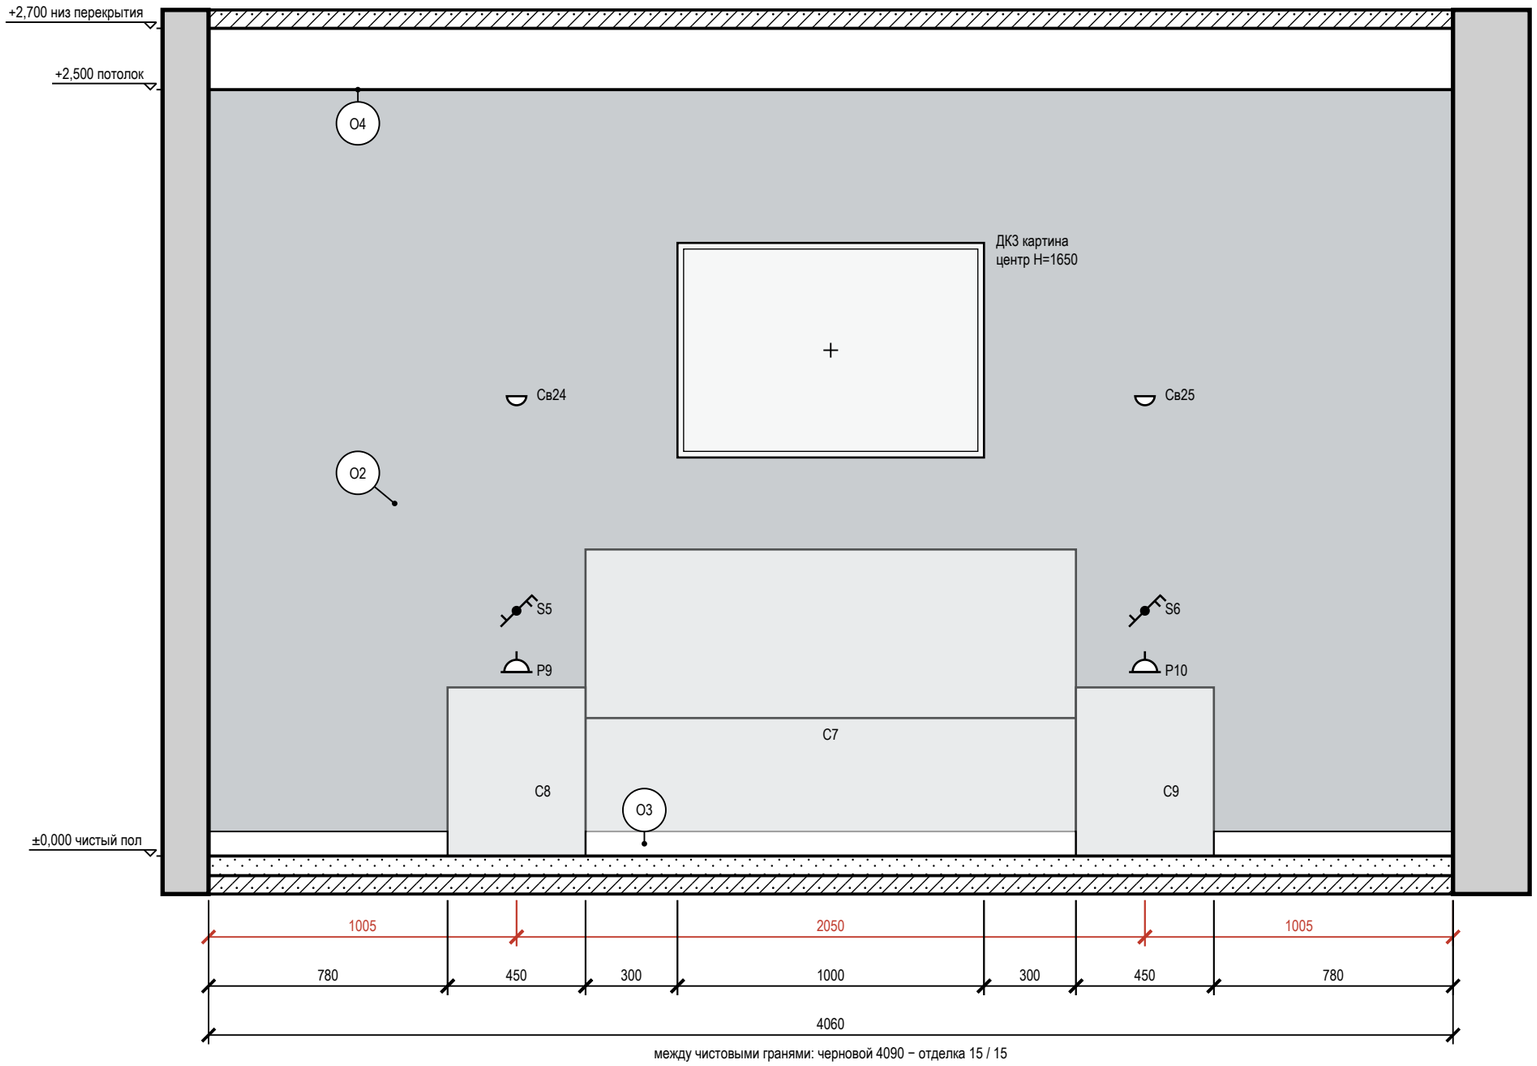

между чистовыми гранями: черновой 4090 − отделка 15 / 15

Ведомость точек и выводов

Марка	Что это	Гр.	Н, мм	От угла, мм	Примечание
P9	розетка: у кровати	5	600	1005	
S5	выключатель	1	800	1005	
Св24	светильник настенный	1	1500	1005	
P10	розетка: у кровати	5	600	3055	
S6	выключатель	1	800	3055	
Св25	светильник настенный	1	1500	3055	

Условные обозначения

- розетка с заземляющим контактом; у знака — марка, ×N постов в рамке, гр. — группа щита, Н — высота оси, мм
- выключатель одноклавишный
- выключатель двухклавишный (флажков — по числу клавиш)
- выключатель с проходной или перекрёстной клавишей (обратный флажок); тип клавиши — в подписи
- светильник настенный (бра), Н — высота оси
- привязки точек и выводов от угла и от пола, мм
- мебель и приборы — фасад по расстановке (условно)
- картина (декор): марка Д, крест — центр, Н — высота центра, мм
- стены и перекрытия в сечении
- окраска: тон — цвет по коду производителя (условно)
- О1 — марка отделки по реестру отделки альбома
- А — марка развёртки: буква стены, стрелка — взгляд

Ведомость отделки (на листе)

Марка	Поверхность	Материал, изделие	Цвет, код	Кол.
О2	акцентная стена	окраска, Farrow & Ball Modern Emulsion, матовая, подготовка Q3	Farrow & Ball No. 30 «Hague Blue»	10,2 м²
О3	плинтус	плинтус МДФ, h 80 мм, аналог: плинтус МДФ под покраску 80×16	Farrow & Ball No. 241 «Skimming Stone»	3,2 м
О4	потолок	окраска, Tikkurila Anti-Reflex 2, глубокоматовая, подготовка Q3	Tikkurila V503 «Winter»	12,8 м²

Примечания

1. Развёртки — вид на стену изнутри помещения, по часовой стрелке; расположение — на листе 89; размеры — в мм по чистовым поверхностям; отметки — в м от ±0,000; высоты Н — от чистого пола помещения до оси изделия, у декора — до центра.
2. Красная цепочка — привязки электроточек и выводов по осям от угла чистовых стен; высота Н — у знака, от чистого пола до оси; высоты мебели, проёмов и границ отделки — колонкой отметок слева. У знака — короткая марка; назначение, группа щита, высота и привязка каждой точки и вывода — в «Ведомости точек и выводов» под видами (каждая точка — строка).
3. У знака электроточки: марка (Р — розетка, S — выключатель, Св — светильник, ЭВ — вывод кабеля), ×N — число постов в рамке, гр. — группа щита, Н — высота оси от чистого пола, мм; группы по клавишам выключателя — на листе выключателей.
4. Схема мебели, приборов и декора не является технической документацией для производства мебели; габариты — по паспортам изделий.
5. Картины и зеркала крепить к основанию по паспорту изделия (закладные и анкеры — в перечне скрытых работ); крест — ось центра предмета.
6. Потолок — у каждой стены свой, по плану потолков (ПТ1); ступени — зоной, кромка короба перед нишей — тонкой линией; в поле потолка: ПТ2 +2,600.

Допущения и предложения на листе. Основа листа: размеры сняты со скана плана заказчика по размерным цепочкам, контрольный обмер на объекте не выполнялся (К-13); высота потолка 2700 мм принята: на плане заказчика не указана (К-11); толщины стен приняты: наружные 250 мм, перегородки 150 мм (на плане 85–190 мм) (К-13); разрешённая мощность 15 кВт принята по типовой квартире, технических условий нет (К-14); утолщение стены 190 × 1360 мм и элемент 1470 × 160 мм плана заказчика не определены (К-12); ниши санузла 2 закрыты перегородкой и фальш-стеной: проектное решение, на плане заказчика ниша у входа открыта (К-18); несущие стены не определены: до технического заключения все существующие стены считаются несущими (К-20); окна существующие и сохраняются; подоконная доска и глубина откосов не заданы — приняты, не замерены (К-27); подрайон климата не задан — принят не северный (жилые от 2,5 м) (К-29). Знак «*» — принято, не замерено (замерить): К-13: отметка существующего пола. См. лист открытых вопросов (лист 7, записи К-11–К-14, К-18, К-20; лист 8, записи К-27, К-29).

1000 мм · печать 1:1

Изм.	Кол.уч	Лист	№ док.	Подп.	Дата
Разраб.		Кырлан А.С.			13.11.26
Пров.					
ГИП					
Н. контр.					
Утв.					

ГД-2026-003-АИ

Трёхкомнатная квартира

Общая площадь 78,95* м² · * размеры со скана, не замерены (реестр — л. 6–11, К-13)

Дизайн-проект интерьера трёхкомнатной квартиры

Стадия	Лист	Листов
РП	98	132

Развёртка стены А. Спальня 2 (пом. 4)

М 1:20

Кырлан Александр Сергеевич


выпуск 13.11.2026 № 6f3a8abb2c · стр. 107 из 157

Развёртка стены Б. Спальня 2 (пом. 4)

Спальня 2 (пом. 4) · вид изнутри помещения · размеры в мм, отметки в м

ПРЕДВАРИТЕЛЬНО · не для производства работ · открыто пунктов: 28 (реестр — л. 6–11)

Стена Б (М 1:20)

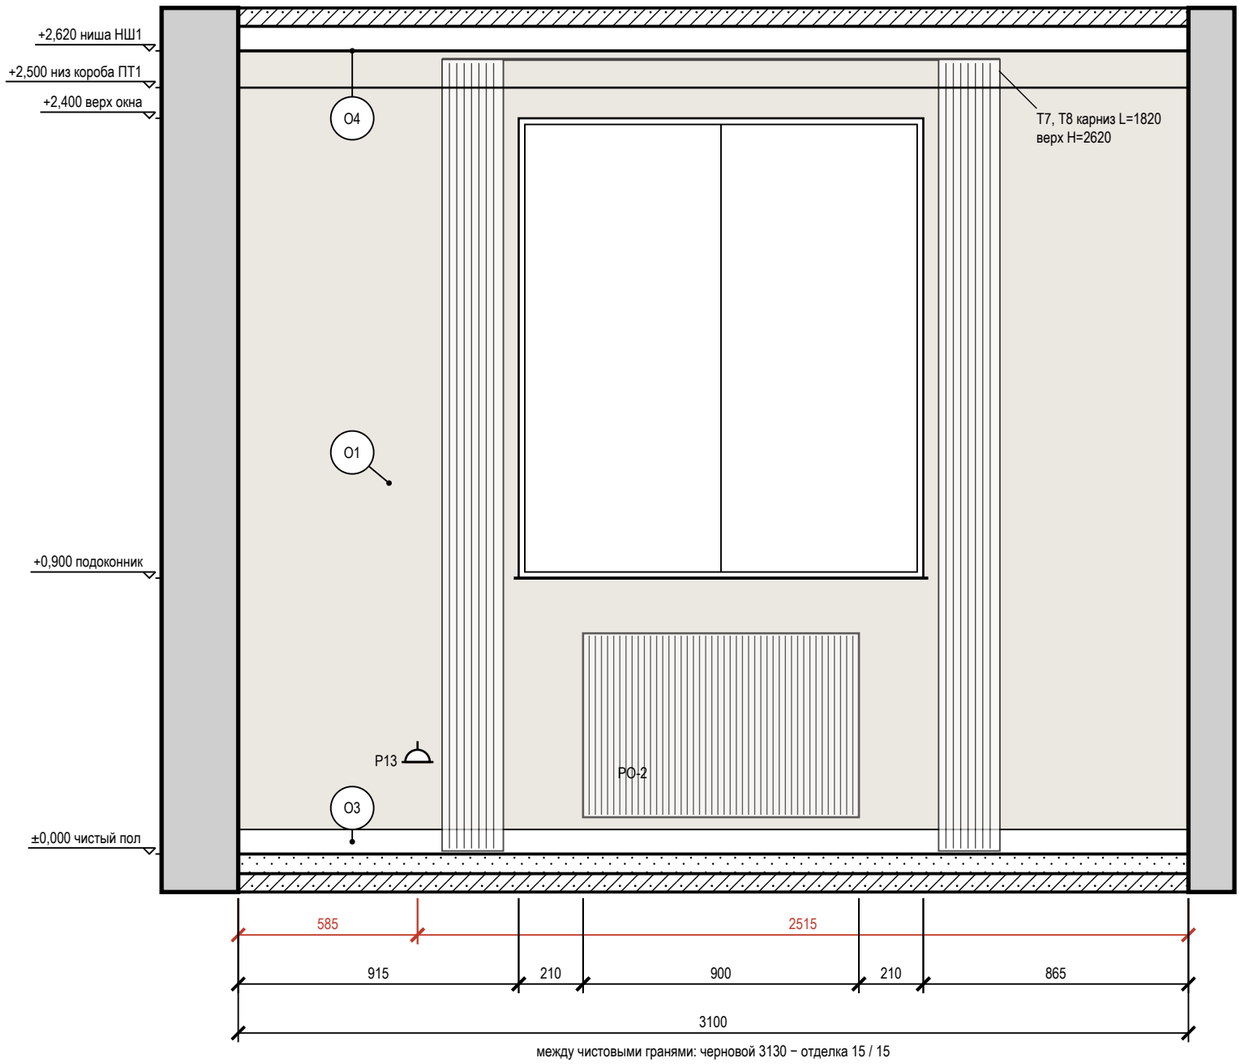

между чистовыми гранями: черновой 3130 − отделка 15 / 15

Ведомость точек и выводов

Марка	Что это	Гр.	H, мм	От угла, мм	Примечание
Р13	розетка: уборка	5	300	585	


Условные обозначения

- розетка с заземляющим контактом; у знака — марка, ×N постов в рамке, гр. — группа щита, H — высота оси, мм
- привязки точек и выводов от угла и от пола, мм
- мебель и приборы — фасад по расстановке (условно)
- карниз (шина) и шторы в собранном виде: марка T, длина L, верх H
- окно: проём, рама, подоконник
- радиатор отопления; марка — по плану отопления
- стены и перекрытия в сечении
- окраска: тон — цвет по коду производителя (условно)
- О1 — марка отделки по реестру отделки альбома
- A — марка развёртки: буква стены, стрелка — взгляд

Ведомость отделки (на листе)

Марка	Поверхность	Материал, изделие	Цвет, код	Кол.
О1	стены	окраска, Farrow & Ball Modern Emulsion, матовая, подготовка Q3	Farrow & Ball No. 241 «Skimming Stone»	6,1 м²
О3	плинтус	плинтус МДФ, h 80 мм, аналог: плинтус МДФ под покраску 80×16	Farrow & Ball No. 241 «Skimming Stone»	3,1 м
О4	потолок	окраска, Tikkurila Anti-Reflex 2, глубокоматовая, подготовка Q3	Tikkurila V503 «Winter»	12,8 м²

Схема развёрток (М 1:100)

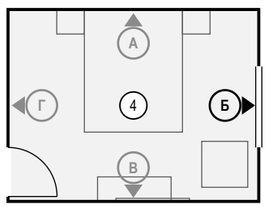

Допущения и предложения на листе. Основа листа: размеры сняты со скана плана заказчика по размерным цепочкам, контрольный обмер на объекте не выполнялся (К-13); высота потолка 2700 мм принята: на плане заказчика не указана (К-11); толщины стен приняты: наружные 250 мм, перегородки 150 мм (на плане 85–190 мм) (К-13); разрешённая мощность 15 кВт принята по типовой квартире, технических условий нет (К-14); утолщение стены 190 × 1360 мм и элемент 1470 × 160 мм плана заказчика не определены (К-12); ниши санузла 2 закрыты перегородкой и фальш-стеной: проектное решение, на плане заказчика ниша у входа открыта (К-18); несущие стены не определены: до технического заключения все существующие стены считаются несущими (К-20); окна существующие и сохраняются; подоконная доска и глубина откосов не заданы — приняты, не замерены (К-27); подрайон климата не задан — принят не северный (жилые от 2,5 м) (К-29). Знак «*» — принято, не замерено и не подтверждено (замерить на объекте): К-13: отметка существующего пола — отметка существующего пола и верха плиты не замерена: на плане заказчика отметок нет; нивелировка — в задании на обмер (К-13). См. лист открытых вопросов (лист 7, записи К-11–К-14, К-18, К-20; лист 8, записи К-27, К-29).

Ведомость изделий и проёмов (на листе)

Марка	Изделие, проём	На виде Ш×В, мм	Низ, мм
РО-2	радиатор отопления	900×600	120

Примечания

1. Развёртки — вид на стену изнутри помещения, по часовой стрелке; расположение — на схеме листа и на листе 89; размеры — в мм по чистовым поверхностям; отметки — в м от ±0,000; высоты H — от чистого пола помещения до оси изделия, у декора — до центра.
2. Красная цепочка — привязки электроточек и выводов по осям от угла чистовых стен; высота H — у знака, от чистого пола до оси; высоты мебели, проёмов и границ отделки — колонкой отметок слева. У знака — короткая марка; назначение, группа щита, высота и привязка каждой точки и вывода — в «Ведомости точек и выводов» под видами (каждая точка — строка).
3. У знака электроточки: марка (Р — розетка, S — выключатель, Св — светильник, ЭВ — вывод кабеля), ×N — число постов в рамке, гр. — группа щита, H — высота оси от чистого пола, мм; группы по клавишам выключателя — на листе выключателей.
4. Схема мебели, приборов и декора не является технической документацией для производства мебели; габариты — по паспортам изделий.
5. Карнизы (шины) — по ведомости текстиля декоратора: длина L и верх H на развёртке — те же числа, что в ведомости; крепление — до окраски потолка.
6. Потолок — у каждой стены свой, по плану потолков (НШ1, ПТ1); ступени — зоной, кромка короба перед нишей — тонкой линией; в поле потолка: ПТ2 +2,600.

1000 мм · печать 1:1

Изм.	Кол.уч	Лист	№ док.	Подп.	Дата
Разраб.		Кырлан А.С.			13.11.26
Пров.					
ГИП					
Н. контр.					
Утв.					

ГД-2026-003-АИ

Трёхкомнатная квартира

Общая площадь 78,95* м² · * размеры со скана, не замерены (реестр — л. 6–11, К-13)

Дизайн-проект интерьера трёхкомнатной квартиры

Стадия	Лист	Листов
РП	99	132

Развёртка стены Б. Спальня 2 (пом. 4)

М 1:20

Кырлан Александр Сергеевич


выпуск 13.11.2026 № 6f3a8abb2c · стр. 108 из 157

Развёртка стены В. Спальня 2 (пом. 4)

Спальня 2 (пом. 4) · вид изнутри помещения · размеры в мм, отметки в м

ПРЕДВАРИТЕЛЬНО · не для производства работ · открыто пунктов: 28 (реестр — л. 6–11)

Стена В (М 1:20)

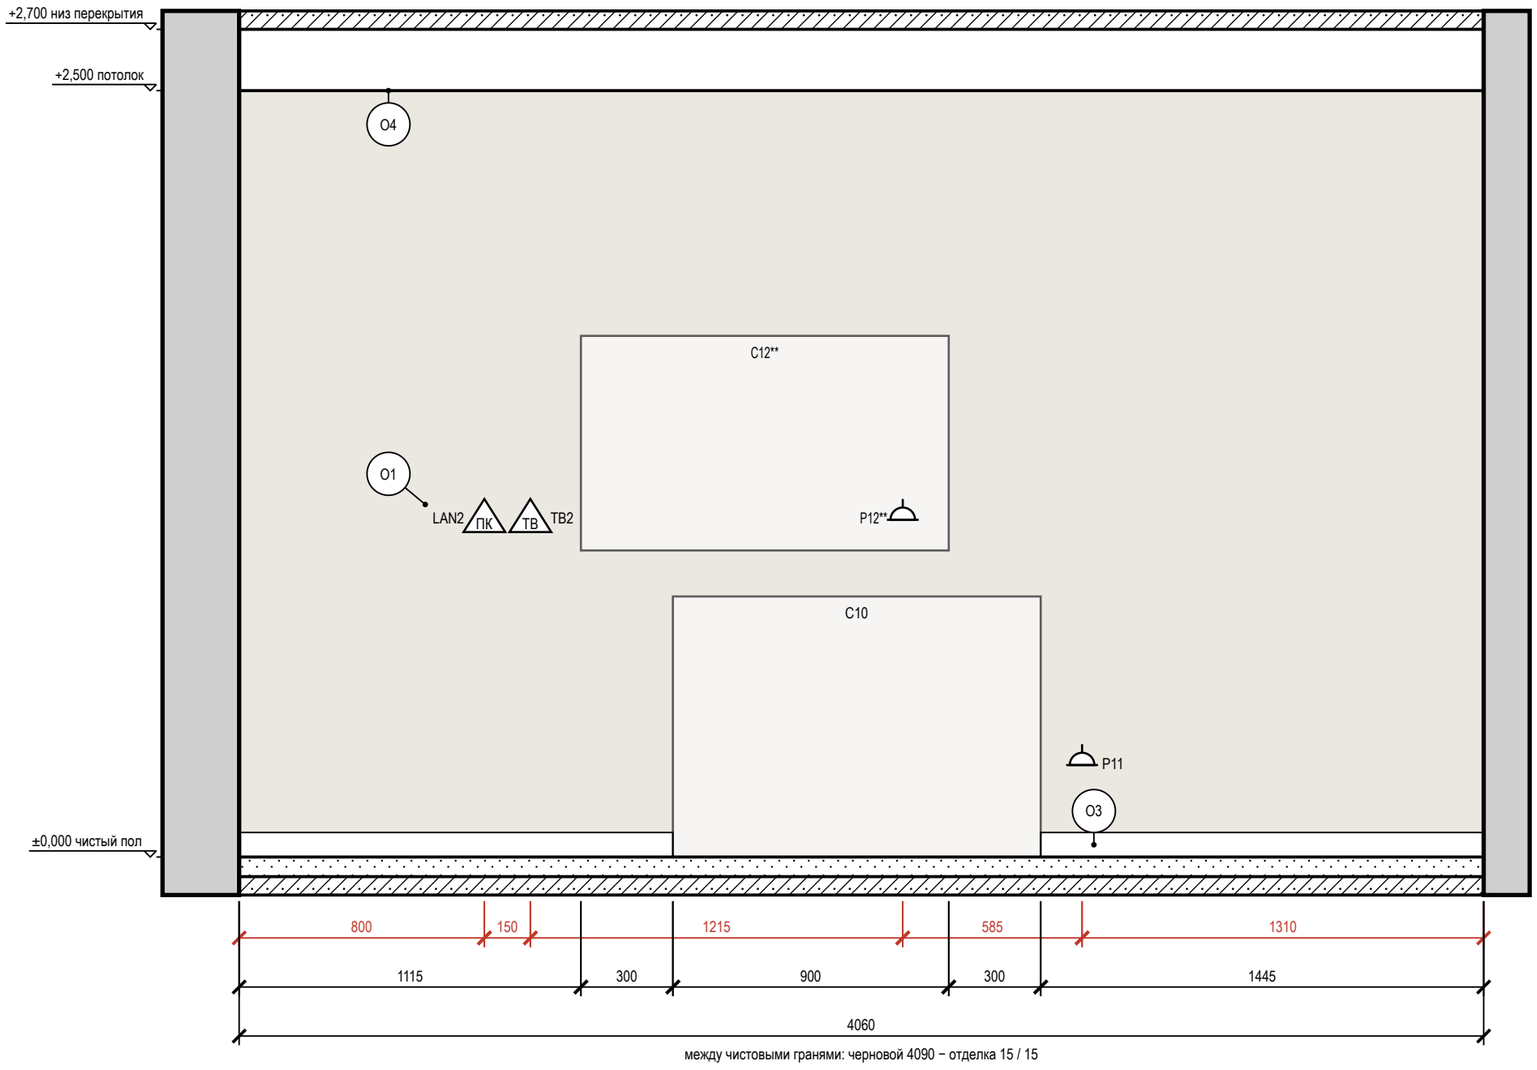

между чистовыми гранями: черновой 4090 − отделка 15 / 15

Ведомость точек и выводов

Марка	Что это	Гр.	Н, мм	От угла, мм	Примечание
LAN2	розетка RJ45: Smart TV (правее телевизора С12**)		1100	800	
ТВ2	розетка ТВ: ТВ над комодом (правее телевизора С12**)		1100	950	
Р12**	розетка: ТВ над комодом (в одной зоне с ТВ2, LAN2)	5	1100	2165	
Р11	розетка: у комода	5	300	2750	

Условные обозначения

- розетка с заземляющим контактом; у знака — марка, ×N постов в рамке, гр. — группа щита, Н — высота оси, мм
- ПК — розетка компьютерная RJ45
- ТВ — розетка телевизионная
- привязки точек и выводов от угла и от пола, мм
- мебель и приборы — фасад по расстановке (условно)
- стены и перекрытия в сечении
- окраска: тон — цвет по коду производителя (условно)
- О1 — марка отделки по реестру отделки альбома
- А — марка развёртки: буква стены, стрелка — взгляд

Ведомость отделки (на листе)

Марка	Поверхность	Материал, изделие	Цвет, код	Кол.
О1	стены	окраска, Farrow & Ball Modern Emulsion, матовая, подготовка Q3	Farrow & Ball No. 241 «Skimming Stone»	10,2 м²
О3	плинтус	плинтус МДФ, h 80 мм, аналог: плинтус МДФ под покраску 80×16	Farrow & Ball No. 241 «Skimming Stone»	2,9 м
О4	потолок	окраска, Tikkurila Anti-Reflex 2, глубокоматовая, подготовка Q3	Tikkurila V503 «Winter»	12,8 м²

Примечания

1. Развёртки — вид на стену изнутри помещения, по часовой стрелке; расположение — на листе 89; размеры — в мм по чистовым поверхностям; отметки — в м от ±0,000; высоты Н — от чистого пола помещения до оси изделия, у декора — до центра.
2. Красная цепочка — привязки электроточек и выводов по осям от угла чистовых стен; высота Н — у знака, от чистого пола до оси; высоты мебели, проёмов и границ отделки — колонкой отметок слева. У знака — короткая марка; назначение, группа щита, высота и привязка каждой точки и вывода — в «Ведомости точек и выводов» под видами (каждая точка — строка).
3. У знака электроточки: марка (Р — розетка, S — выключатель, Св — светильник, ЭВ — вывод кабеля), ×N — число постов в рамке, гр. — группа щита, Н — высота оси от чистого пола, мм; группы по клавишам выключателя — на листе выключателей.
4. Схема мебели, приборов и декора не является технической документацией для производства мебели; габариты — по паспортам изделий.
5. Потолок — у каждой стены свой, по плану потолков (ПТ1); ступени — зоной, кромка короба перед нишей — тонкой линией; в поле потолка: ПТ2 +2,600.

Допущения и предложения на листе. Основа листа: размеры сняты со скана плана заказчика по размерным цепочкам, контрольный обмер на объекте не выполнялся (К-13); высота потолка 2700 мм принята: на плане заказчика не указана (К-11); толщины стен приняты: наружные 250 мм, перегородки 150 мм (на плане 85–190 мм) (К-13); разрешённая мощность 15 кВт принята по типовой квартире, технических условий нет (К-14); утолщение стены 190 × 1360 мм и элемент 1470 × 160 мм плана заказчика не определены (К-12); ниши санузла 2 закрыты перегородкой и фальш-стеной: проектное решение, на плане заказчика ниша у входа открыта (К-18); несущие стены не определены: до технического заключения все существующие стены считаются несущими (К-20); окна существующие и сохраняются; подоконная доска и глубина откосов не заданы — приняты, не замерены (К-27); подрайон климата не задан — принят не северный (жилые от 2,5 м) (К-29). Знак «*» — принято, не замерено (замерить): К-13: отметка существующего пола. Знак «**» — предложено, не утверждено (согласовать): К-7: С12, Р12. См. лист открытых вопросов (лист 6, запись К-7; лист 7, записи К-11–К-14, К-18, К-20; лист 8, записи К-27, К-29).

1000 мм · печать 1:1

Изм.	Кол.уч	Лист	№ док.	Подп.	Дата
Разраб.		Кырлан А.С.			13.11.26
Пров.					
ГИП					
Н. контр.					
Утв.					

ГД-2026-003-АИ

Трёхкомнатная квартира

Общая площадь 78,95* м² · * размеры со скана, не замерены (реестр — л. 6–11, К-13)

Дизайн-проект интерьера трёхкомнатной квартиры

Стадия	Лист	Листов
РП	100	132

Развёртка стены В. Спальня 2 (пом. 4)

М 1:20

Кырлан Александр Сергеевич


выпуск 13.11.2026 № 6f3a8abb2c · стр. 109 из 157

Развёртка стены Г. Спальня 2 (пом. 4)

Спальня 2 (пом. 4) · вид изнутри помещения · размеры в мм, отметки в м

ПРЕДВАРИТЕЛЬНО · не для производства работ · открыто пунктов: 28 (реестр — л. 6–11)

Стена Г (М 1:20)

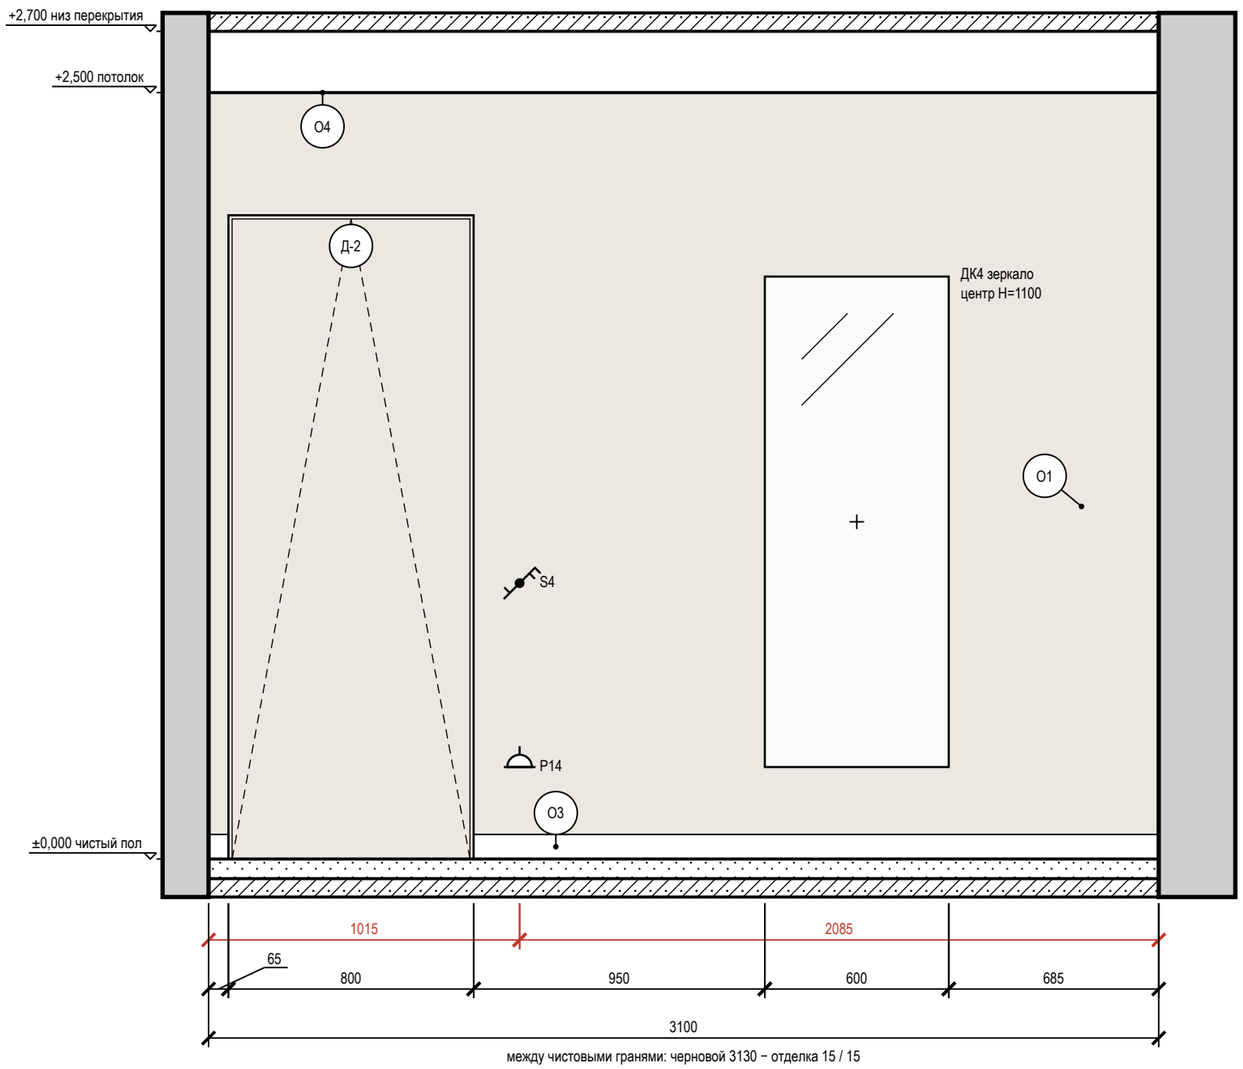

между чистовыми гранями: черновой 3130 − отделка 15 / 15

Ведомость точек и выводов

Марка	Что это	Гр.	Н, мм	От угла, мм	Примечание
Р14	розетка: уборка у входа	5	300	1015	
S4	выключатель	1	900	1015	


Условные обозначения

- розетка с заземляющим контактом; у знака — марка, ×N постов в рамке, гр. — группа щита, Н — высота оси, мм
- выключатель одноклавишный
- выключатель двухклавишный (флажков — по числу клавиш)
- выключатель с проходной или перекрёстной клавишей (обратный флажок); тип клавиши — в подписи
- привязки точек и выводов от угла и от пола, мм
- мебель и приборы — фасад по расстановке (условно)
- зеркало: марка Д, крест — центр, Н — высота центра, мм
- дверь скрытого монтажа: полотно в плоскости стены (узел — на листе узлов)
- стены и перекрытия в сечении
- окраска: тон — цвет по коду производителя (условно)
- О1 — марка отделки по реестру отделки альбома
- А — марка развёртки: буква стены, стрелка — взгляд

Ведомость отделки (на листе)

Марка	Поверхность	Материал, изделие	Цвет, код	Кол.
О1	стены	окраска, Farrow & Ball Modern Emulsion, матовая, подготовка Q3	Farrow & Ball No. 241 «Skimming Stone»	6,1 м²
О3	плинтус	плинтус МДФ, h 80 мм, аналог: плинтус МДФ под покраску 80×16	Farrow & Ball No. 241 «Skimming Stone»	2,3 м
О4	потолок	окраска, Tikkurila Anti-Reflex 2, глубокоматовая, подготовка Q3	Tikkurila V503 «Winter»	12,8 м²

Схема развёрток (М 1:100)

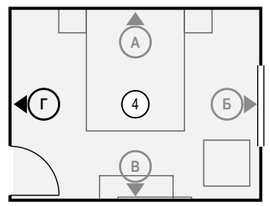

Примечания

1. Развёртки — вид на стену изнутри помещения, по часовой стрелке; расположение — на схеме листа и на листе 89; размеры — в мм по чистовым поверхностям; отметки — в м от ±0,000; высоты Н — от чистого пола помещения до оси изделия, у декора — до центра.
2. Красная цепочка — привязки электроточек и выводов по осям от угла чистовых стен; высота Н — у знака, от чистого пола до оси; высоты мебели, проёмов и границ отделки — колонкой отметок слева. У знака — короткая марка; назначение, группа щита, высота и привязка каждой точки и вывода — в «Ведомости точек и выводов» под видами (каждая точка — строка).
3. У знака электроточки: марка (Р — розетка, S — выключатель, Св — светильник, ЭВ — вывод кабеля), ×N — число постов в рамке, гр. — группа щита, Н — высота оси от чистого пола, мм; группы по клавишам выключателя — на листе выключателей.
4. Схема мебели, приборов и декора не является технической документацией для производства мебели; габариты — по паспортам изделий.
5. Картины и зеркала крепить к основанию по паспорту изделия (закладные и анкеры — в перечне скрытых работ); крест — ось центра предмета.
6. Двери скрытого монтажа — полотно в плоскости стены, отделка стены по полотну, плинтус прерывается у короба (узел — на листе узлов).
7. Потолок — у каждой стены свой, по плану потолков (ПТ1); ступени — зоной, кромка короба перед нишей — тонкой линией; в поле потолка: ПТ2 +2,600.

Допущения и предложения на листе. Основа листа: размеры сняты со скана плана заказчика по размерным цепочкам, контрольный обмер на объекте не выполнялся (К-13); высота потолка 2700 мм принята: на плане заказчика не указана (К-11); толщины стен приняты: наружные 250 мм, перегородки 150 мм (на плане 85–190 мм) (К-13); разрешённая мощность 15 кВт принята по типовой квартире, технических условий нет (К-14); утолщение стены 190 × 1360 мм и элемент 1470 × 160 мм плана заказчика не определены (К-12); ниши санузла 2 закрыты перегородкой и фальш-стеной: проектное решение, на плане заказчика ниша у входа открыта (К-18); несущие стены не определены: до технического заключения все существующие стены считаются несущими (К-20); окна существующие и сохраняются; подоконная доска и глубина откосов не заданы — приняты, не замерены (К-27); подрайон климата не задан — принят не северный (жилые от 2,5 м) (К-29). Знак «*» — принято, не замерено (замерить): К-13: отметка существующего пола. См. лист открытых вопросов (лист 7, записи К-11–К-14, К-18, К-20; лист 8, записи К-27, К-29).

1000 мм · печать 1:1

Изм.	Кол.уч	Лист	№ док.	Подп.	Дата
Разраб.		Кырлан А.С.			13.11.26
Пров.					
ГИП					
Н. контр.					
Утв.					

ГД-2026-003-АИ

Трёхкомнатная квартира

Общая площадь 78,95* м² · * размеры со скана, не замерены (реестр — л. 6–11, К-13)

Дизайн-проект интерьера трёхкомнатной квартиры

Стадия	Лист	Листов
РП	101	132

Развёртка стены Г. Спальня 2 (пом. 4)

М 1:20


Кырлан Александр Сергеевич

выпуск 13.11.2026 № 6f3a8abb2c · стр. 110 из 157

Развёртка стены А. Прихожая (пом. 5)

Прихожая (пом. 5) · вид изнутри помещения · размеры в мм, отметки в м

Стена А (М 1:20)

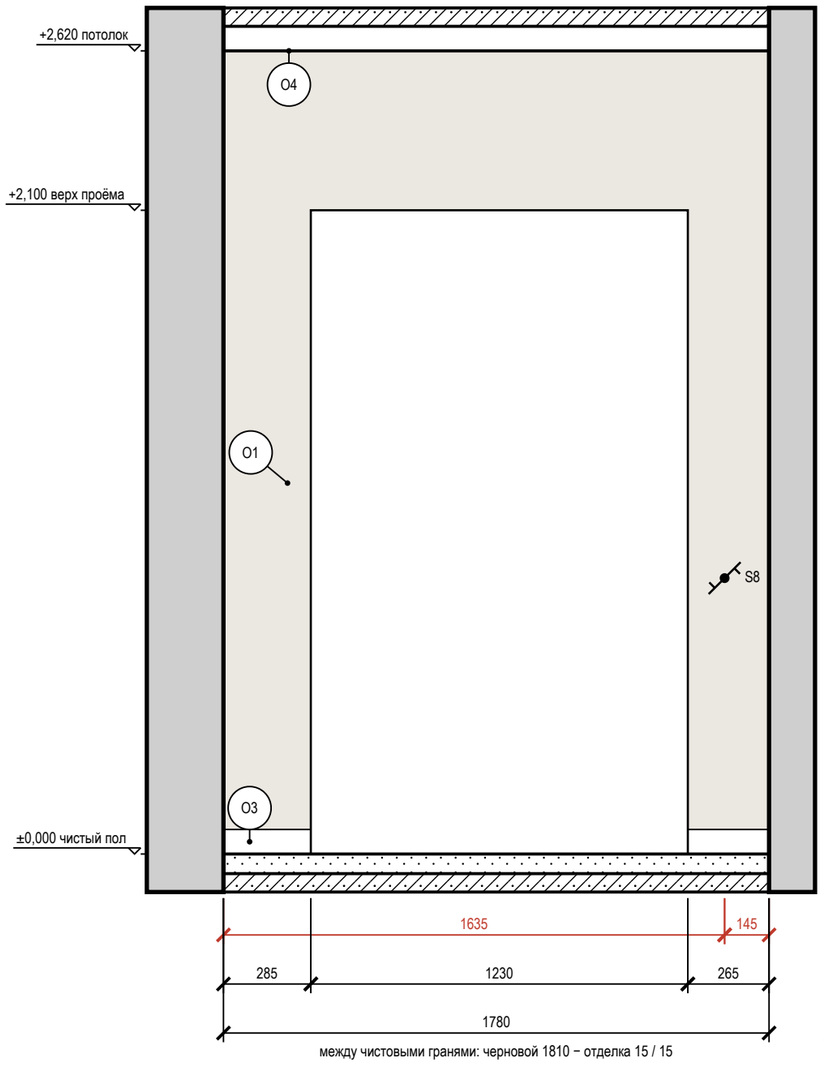

между чистовыми гранями: черновой 1810 − отделка 15 / 15

Допущения и предложения на листе

Основа листа: размеры сняты со скана плана заказчика по размерным цепочкам, контрольный обмер на объекте не выполнялся (К-13); высота потолка 2700 мм принята: на плане заказчика не указана (К-11); толщины стен приняты: наружные 250 мм, перегородки 150 мм (на плане 85–190 мм) (К-13); разрешённая мощность 15 кВт принята по типовой квартире, технических условий нет (К-14); утолщение стены 190 × 1360 мм и элемент 1470 × 160 мм плана заказчика не определены (К-12); ниши санузла 2 закрыты перегородкой и фальш-стеной: проектное решение, на плане заказчика ниша у входа открыта (К-18); несущие стены не определены: до технического заключения все существующие стены считаются несущими (К-20); окна существующие и сохраняются; подоконная доска и глубина откосов не заданы — приняты, не замерены (К-27); подрайон климата не задан — принят не северный (жилые от 2,5 м) (К-29).

Знак «*» — принято, не замерено и не подтверждено (замерить на объекте): К-13: отметка существующего пола — отметка существующего пола и верха плиты не замерена: на плане заказчика отметок нет; нивелировка — в задании на обмер (К-13); К-26: дверь пом. 5 (стена В) — входная дверь существующая; по плану заказчика полотно открывается наружу, в общий коридор — направление взято с плана и на объекте не проверено; остаётся ли существующий блок или он заменяется — не решено (К-26).

См. лист открытых вопросов (лист 7, записи К-11–К-14, К-18, К-20; лист 8, записи К-26, К-27, К-29).

Ведомость точек и выводов

Марка	Что это	Гр.	Н, мм	От угла, мм	Примечание
S8	выключатель	2	900	1635	


Условные обозначения

- выключатель одноклавишный
- выключатель с проходной или перекрёстной клавишей (обратный флажок); тип клавиши — в подписи
- привязки точек и выводов от угла и от пола, мм
- мебель и приборы — фасад по расстановке (условно)
- дверной проём; марка двери — в кружке
- стены и перекрытия в сечении
- окраска: тон — цвет по коду производителя (условно)
- О1 — марка отделки по реестру отделки альбома
- А — марка развёртки: буква стены, стрелка — взгляд

Ведомость отделки (на листе)

Марка	Поверхность	Материал, изделие	Цвет, код	Кол.
О1	стены	окраска, Farrow & Ball Modern Emulsion, матовая, подготовка Q3	Farrow & Ball No. 241 «Skimming Stone»	2,1 м²
О3	плинтус	плинтус МДФ, h 80 мм, аналог: плинтус МДФ под покраску 80×16	Farrow & Ball No. 241 «Skimming Stone»	0,6 м
О4	потолок	окраска, Tikkurila Anti-Reflex 2, глубокоматовая, подготовка Q3	Tikkurila V503 «Winter»	7,1 м²

Схема развёрток (М 1:100)

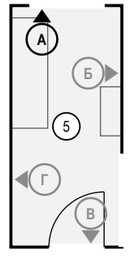

Примечания

1. Развёртки — вид на стену изнутри помещения, по часовой стрелке; расположение — на схеме листа и на листе 89; размеры — в мм по чистовым поверхностям; отметки — в м от ±0,000; высоты Н — от чистого пола помещения до оси изделия, у декора — до центра.
2. Красная цепочка — привязки электроточек и выводов по осям от угла чистовых стен; высота Н — у знака, от чистого пола до оси; высоты мебели, проёмов и границ отделки — колонкой отметок слева. У знака — короткая марка; назначение, группа щита, высота и привязка каждой точки и вывода — в «Ведомости точек и выводов» под видами (каждая точка — строка).
3. У знака электроточки: марка (Р — розетка, S — выключатель, Св — светильник, ЭВ — вывод кабеля), ×N — число постов в рамке, гр. — группа щита, Н — высота оси от чистого пола, мм; группы по клавишам выключателя — на листе выключателей.
4. Схема мебели, приборов и декора не является технической документацией для производства мебели; габариты — по паспортам изделий.

1000 мм · печать 1:1

Изм.	Кол.уч	Лист	№ док.	Подп.	Дата
Разраб.		Кырлан А.С.			13.11.26
Пров.					
ГИП					
Н. контр.					
Утв.					

ГД-2026-003-АИ

Трёхкомнатная квартира

Общая площадь 78,95* м² · * размеры со скана, не замерены (реестр — л. 6–11, К-13)

Дизайн-проект интерьера трёхкомнатной квартиры

Стадия	Лист	Листов
РП	102	132

Развёртка стены А. Прихожая (пом. 5)

М 1:20

Кырлан Александр Сергеевич


выпуск 13.11.2026 № 6f3a8abb2c · стр. 111 из 157

Развёртки стен Б, В. Прихожая (пом. 5)

Прихожая (пом. 5) · вид изнутри помещения · размеры в мм, отметки в м


ПРЕДВАРИТЕЛЬНО · не для производства работ · открыто пунктов: 28 (реестр — л. 6–11)

Стена Б (М 1:25)

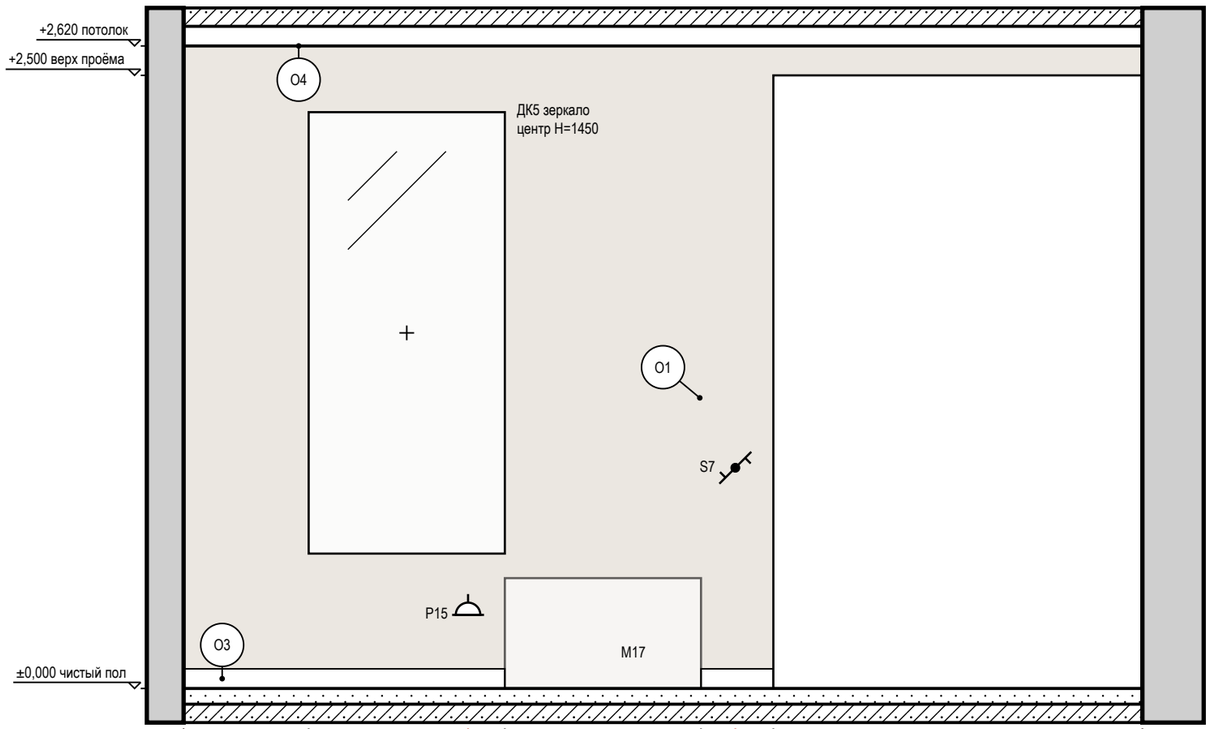


между чистовыми гранями: черновой 3940 − отделка 15 / 15

Стена В (М 1:25)

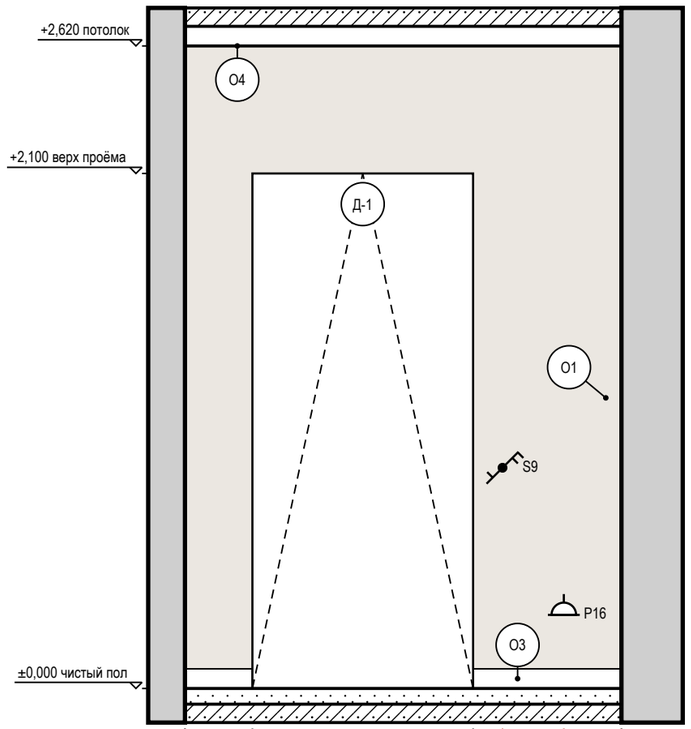

между чистовыми гранями: черновой 1810 − отделка 15 / 15

Схема развёрток (М 1:50)

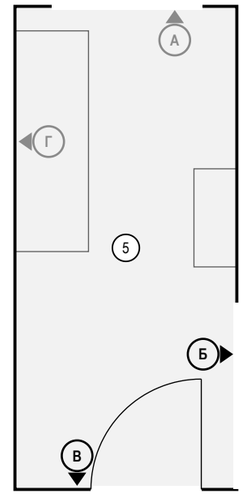

Ведомость точек и выводов

Стена	Марка	Что это	Гр.	Н, мм	От угла, мм	Примечание
Б	Р15	розетка: пылесос, сушилка обуви	6	300	1160	
Б	S7	выключатель	2	900	2250	
В	S9	выключатель	2	900	1295	
В	Р16	розетка: уборка	6	300	1545	

Условные обозначения

- розетка с заземляющим контактом; у знака — марка, ×N постов в рамке, гр. — группа щита, Н — высота оси, мм
- выключатель одноклавишный
- выключатель двухклавишный (флажков — по числу клавиш)
- выключатель с проходной или перекрёстной клавишей (обратный флажок); тип клавиши — в подписи
- привязки точек и выводов от угла и от пола, мм
- мебель и приборы — фасад по расстановке (условно)
- зеркало: марка Д, крест — центр, Н — высота центра, мм
- дверной проём; марка двери — в кружке
- стены и перекрытия в сечении
- окраска: тон — цвет по коду производителя (условно)
- О1 — марка отделки по реестру отделки альбома
- А — марка развёртки: буква стены, стрелка — взгляд

Примечания

1. Развёртки — вид на стену изнутри помещения, по часовой стрелке; расположение — на схеме листа и на листе 89; размеры — в мм по чистовым поверхностям; отметки — в м от ±0,000; высоты Н — от чистого пола помещения до оси изделия, у декора — до центра.
2. Красная цепочка — привязки электроточек и выводов по осям от угла чистовых стен; высота Н — у знака, от чистого пола до оси; высоты мебели, проёмов и границ отделки — колонкой отметок слева. У знака — короткая марка; назначение, группа щита, высота и привязка каждой точки и вывода — в «Ведомости точек и выводов» под видами (каждая точка — строка).
3. Отделка стен — по ведомости отделки помещений, лист 67.
4. У знака электроточки: марка (Р — розетка, S — выключатель, Св — светильник, ЭВ — вывод кабеля), ×N — число постов в рамке, гр. — группа щита, Н — высота оси от чистого пола, мм; группы по клавишам выключателя — на листе выключателей.
5. Схема мебели, приборов и декора не является технической документацией для производства мебели; габариты — по паспортам изделий.
6. Картины и зеркала крепить к основанию по паспорту изделия (закладные и анкеры — в перечне скрытых работ); крест — ось центра предмета.

Допущения и предложения на листе. Знак «*» принято (замерить): дверь пом. 5 (стена В), отметка существующего пола. См. лист открытых вопросов (листы 6–11).

1000 мм · печать 1:1

Изм.	Кол.уч	Лист	№ док.	Подп.	Дата
Разраб.		Кырлан А.С.			13.11.26
Пров.					
ГИП					
Н. контр.					
Утв.					

ГД-2026-003-АИ

Трёхкомнатная квартира

Общая площадь 78,95* м² · * размеры со скана, не замерены (реестр — л. 6–11, К-13)

Дизайн-проект интерьера трёхкомнатной квартиры

Стадия	Лист	Листов
РП	103	132

Развёртки стен Б, В. Прихожая (пом. 5)

М 1:25

Кырлан Александр Сергеевич


выпуск 13.11.2026 № 6f3a8abb2c · стр. 112 из 157

Развёртка стены Г. Прихожая (пом. 5)

Прихожая (пом. 5) · вид изнутри помещения · размеры в мм, отметки в м

ПРЕДВАРИТЕЛЬНО · не для производства работ · открыто пунктов: 28 (реестр — л. 6–11)

Стена Г (М 1:25)

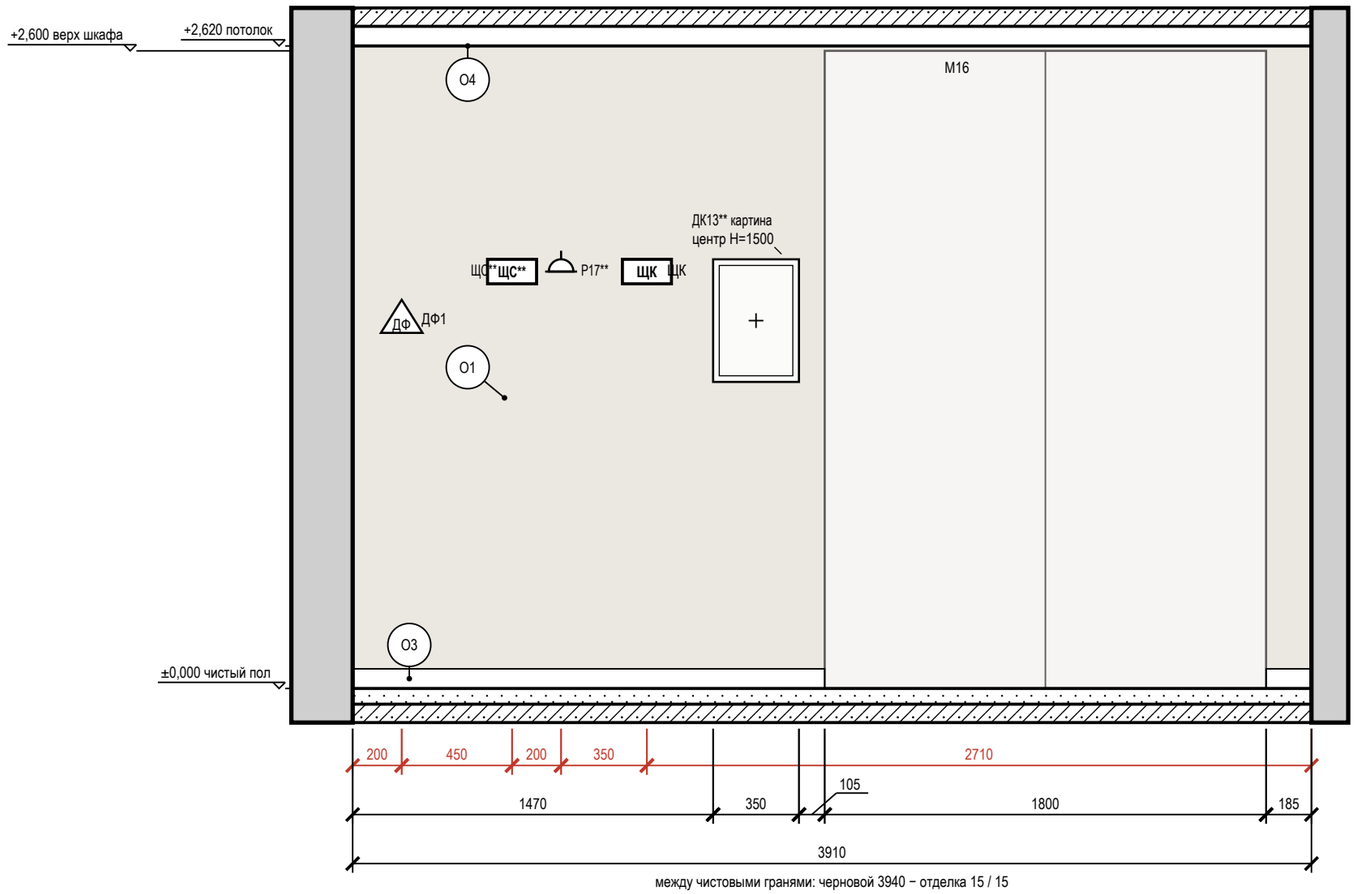

между чистовыми гранями: черновой 3940 − отделка 15 / 15

Ведомость точек и выводов

Марка	Что это	Гр.	Н, мм	От угла, мм	Примечание
ДФ1	домофон: трубка домофона		1500	200	
ЩС**	щит: щит слаботочный: ввод оптики, ONT, роутер, патч-панель		1700	650	
Р17**	розетка: питание слаботочного щита (рядом с ЩС**)	14	1700	850	
ЩК	щит: щит квартирный ЩРВ-П-48		1700	1200	

Условные обозначения

- розетка с заземляющим контактом; у знака марка, ×N — постов в рамке, гр. — группа щита, Н — высота оси, мм
- ДФ — трубка или монитор домофона
- ЩК — щит квартирный
- привязки точек и выводов от угла и от пола, мм
- мебель и приборы — фасад по расстановке (условно)
- картина (декор): марка Д, крест — центр, Н — высота центра, мм
- стены и перекрытия в сечении
- окраска: тон — цвет по коду производителя (условно)
- О1 — марка отделки по реестру отделки альбома
- А — марка развёртки: буква стены, стрелка взгляд

Ведомость отделки (на листе)

Марка	Поверхность	Материал, изделие	Цвет, код	Кол.
О1	стены	окраска, Farrow & Ball Modern Emulsion, матовая, подготовка Q3	Farrow & Ball No. 241 «Skimming Stone»	10,2 м²
О3	плинтус	плинтус МДФ, h 80 мм, аналог: плинтус МДФ под покраску 80×16	Farrow & Ball No. 241 «Skimming Stone»	2,1 м
О4	потолок	окраска, Tikkurila Anti-Reflex 2, глубокоматовая, подготовка Q3	Tikkurila V503 «Winter»	7,1 м²

Ведомость изделий и проёмов (на листе)

Марка	Изделие, проём	На виде Ш×В, мм	Низ, мм
ДК13**	картина	350×500	1250
М16	шкаф-купе	1800×2600	0

Примечания

1. Развёртки — вид на стену изнутри помещения, по часовой стрелке; расположение — на листе 89; размеры — в мм по чистовым поверхностям; отметки — в м от ±0,000; высоты Н — от чистого пола помещения до оси изделия, у декора — до центра.
2. Красная цепочка — привязки электроточек и выводов по осям от угла чистовых стен; высота Н — у знака, от чистого пола до оси; высоты мебели, проёмов и границ отделки — колонкой отметок слева. У знака — короткая марка; назначение, группа щита, высота и привязка каждой точки и вывода — в «Ведомости точек и выводов» под видами (каждая точка — строка).
3. У знака электроточки: марка (Р — розетка, S — выключатель, Св — светильник, ЭВ — вывод кабеля), ×N — число постов в рамке, гр. — группа щита, Н — высота оси от чистого пола, мм; группы по клавишам выключателя — на листе выключателей.
4. Схема мебели, приборов и декора не является технической документацией для производства мебели; габариты — по паспортам изделий.
5. Картины и зеркала крепить к основанию по паспорту изделия (закладные и анкеры — в перечне скрытых работ); крест — ось центра предмета.

Допущения и предложения на листе. Основа листа: размеры сняты со скана плана заказчика по размерным цепочкам, контрольный обмер на объекте не выполнялся (К-13); высота потолка 2700 мм принята: на плане заказчика не указана (К-11); толщины стен приняты: наружные 250 мм, перегородки 150 мм (на плане 85–190 мм) (К-13); разрешённая мощность 15 кВт принята по типовой квартире, технических условий нет (К-14); утолщение стены 190 × 1360 мм и элемент 1470 × 160 мм плана заказчика не определены (К-12); ниши санузла 2 закрыты перегородкой и фальш-стеной: проектное решение, на плане заказчика ниша у входа открыта (К-18); несущие стены не определены: до технического заключения все существующие стены считаются несущими (К-20); окна существующие и сохраняются; подоконная доска и глубина откосов не заданы — приняты, не замерены (К-27); подрайон климата не задан — принят не северный (жилые от 2,5 м) (К-29). Знак «*» — принято, не замерено и не подтверждено (замерить на объекте): К-13: отметка существующего пола — отметка существующего пола и верха плиты не замерена: на плане заказчика отметок нет; нивелировка — в задании на обмер (К-13); К-26: дверь пом. 5 (стена В) — входная дверь существующая; по плану заказчика полотно открывается наружу, в общий коридор — направление взято с плана и на объекте не проверено; остаётся ли существующий блок или он заменяется — не решено (К-26). Знак «**» — предложение проектировщика, заказчиком не утверждено (согласовать с заказчиком): ИЗ-9, ИЗ-17, К-7: ЩС — щит слаботочный: место и состав; К-7: Р17 — высота 1700 мм выше нормы 1 м (ПУЭ 6.6.30) по назначению: питание слаботочного щита ЩС, рядом со щитом на его высоте. См. лист открытых вопросов (лист 6, запись К-7; лист 7, записи К-11–К-14, К-18, К-20; лист 8, записи К-26, К-27, К-29; лист 9, запись ИЗ-9; лист 11, записи ИЗ-17, ИЗ-20).

1000 мм · печать 1:1

Изм.	Кол.уч	Лист	№ док.	Подп.	Дата
Разраб.		Кырлан А.С.			13.11.26
Пров.					
ГИП					
Н. контр.					
Утв.					

ГД-2026-003-АИ

Трёхкомнатная квартира

Общая площадь 78,95* м² · * размеры со скана, не замерены (реестр — л. 6–11, К-13)

Дизайн-проект интерьера трёхкомнатной квартиры

Стадия	Лист	Листов
РП	104	132

Развёртка стены Г. Прихожая (пом. 5)

М 1:25


Кырлан Александр Сергеевич

выпуск 13.11.2026 № 6f3a8abb2c · стр. 113 из 157

Развёртка стены Б2. Кухня-гостиная (пом. 6), кухонный фронт

Кухня-гостиная (пом. 6) · вид изнутри помещения · размеры в мм, отметки в м

Стена Б2 (М 1:20)

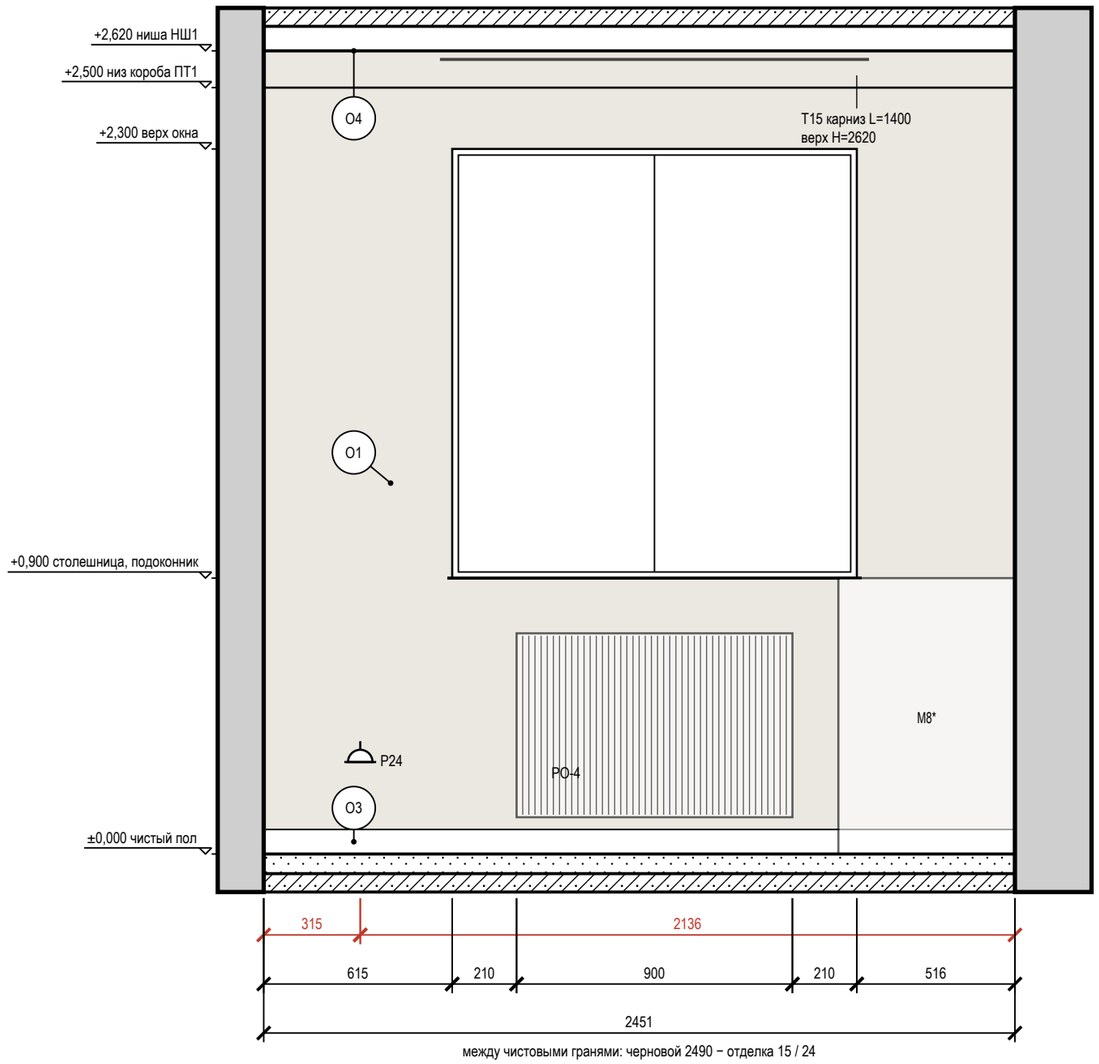

между чистовыми гранями: черновой 2490 − отделка 15 / 24

Ведомость точек и выводов

Марка	Что это	Гр.	H, мм	От угла, мм	Примечание
Р24	розетка: у обеденного стола	6	300	315	


Условные обозначения

- розетка с заземляющим контактом; у знака — марка, ×N постов в рамке, гр. — группа щита, H — высота оси, мм
- привязки точек и выводов от угла и от пола, мм
- мебель и приборы — фасад по расстановке (условно)
- карниз (шина) и шторы в собранном виде: марка T, длина L, верх H
- окно: проём, рама, подоконник
- радиатор отопления; марка — по плану отопления
- стены и перекрытия в сечении
- окраска: тон — цвет по коду производителя (условно)
- О1 — марка отделки по реестру отделки альбома
- А — марка развёртки: буква стены, стрелка — взгляд

Ведомость отделки (на листе)

Марка	Поверхность	Материал, изделие	Цвет, код	Кол.
О1	стены	окраска, Farrow & Ball Modern Emulsion, матовая, подготовка Q3	Farrow & Ball No. 241 «Skimming Stone»	4,6 м²
О3	плинтус	плинтус МДФ, h 80 мм, аналог: плинтус МДФ под покраску 80×16	Farrow & Ball No. 241 «Skimming Stone»	2,5 м
О4	потолок	окраска, Tikkurila Anti-Reflex 2, глубокоматовая, подготовка Q3	Tikkurila V503 «Winter»	29,2 м²

Схема развёрток (М 1:100)

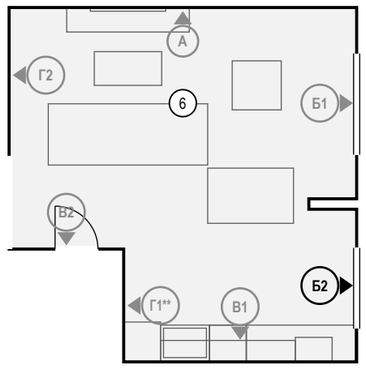

Примечания

1. Развёртки — вид на стену изнутри помещения, по часовой стрелке; расположение — на схеме листа и на листе 89; размеры — в мм по чистовым поверхностям; отметки — в м от ±0,000; высоты H — от чистого пола помещения до оси изделия, у декора — до центра.
2. Красная цепочка — привязки электроточек и выводов по осям от угла чистовых стен; высота H — у знака, от чистого пола до оси; высоты мебели, проёмов и границ отделки — колонкой отметок слева. У знака — короткая марка; назначение, группа щита, высота и привязка каждой точки и вывода — в «Ведомости точек и выводов» под видами (каждая точка — строка).
3. У знака электроточки: марка (Р — розетка, S — выключатель, Св — светильник, ЭВ — вывод кабеля), ×N — число постов в рамке, гр. — группа щита, H — высота оси от чистого пола, мм; группы по клавишам выключателя — на листе выключателей.
4. Схема мебели, приборов и декора не является технической документацией для производства мебели; габариты — по паспортам изделий.
5. Карнизы (шины) — по ведомости текстиля декоратора: длина L и верх H на развёртке — те же числа, что в ведомости; крепление — до окраски потолка.
6. Выводы кухонной техники — по утверждённому проекту кухни: привязки выводов даются от осей модулей гарнитура.
7. Потолок — у каждой стены свой, по плану потолков (НШ1, ПТ1); ступени — зоной, кромка короба перед нишей — тонкой линией; в поле потолка: ПТ2 +2,600.

Допущения и предложения на листе. Знак «*» принято (замерить): отметка существующего пола. Знак «**» предложено (согласовать): дверь пом. 6 (стена В). См. лист открытых вопросов (листы 6–11).

1000 мм · печать 1:1

Изм.	Кол.уч	Лист	№ док.	Подп.	Дата
Разраб.		Кырлан А.С.			13.11.26
Пров.					
ГИП					
Н. контр.					
Утв.					

ГД-2026-003-АИ

Трёхкомнатная квартира

Общая площадь 78,95* м² · * размеры со скана, не замерены (реестр — л. 6–11, К-13)

Дизайн-проект интерьера трёхкомнатной квартиры

Стадия	Лист	Листов
РП	105	132

Развёртка стены Б2. Кухня-гостиная (пом. 6), кухонный фронт

М 1:20

Кырлан Александр Сергеевич


выпуск 13.11.2026 № 6f3a8abb2c · стр. 114 из 157

Развёртка стены В1. Кухня-гостиная (пом. 6), кухонный фронт

Кухня-гостиная (пом. 6) · вид изнутри помещения · размеры в мм, отметки в м

ПРЕДВАРИТЕЛЬНО · не для производства работ · открыто пунктов: 28 (реестр — л. 6–11)

Стена В1 (М 1:20)

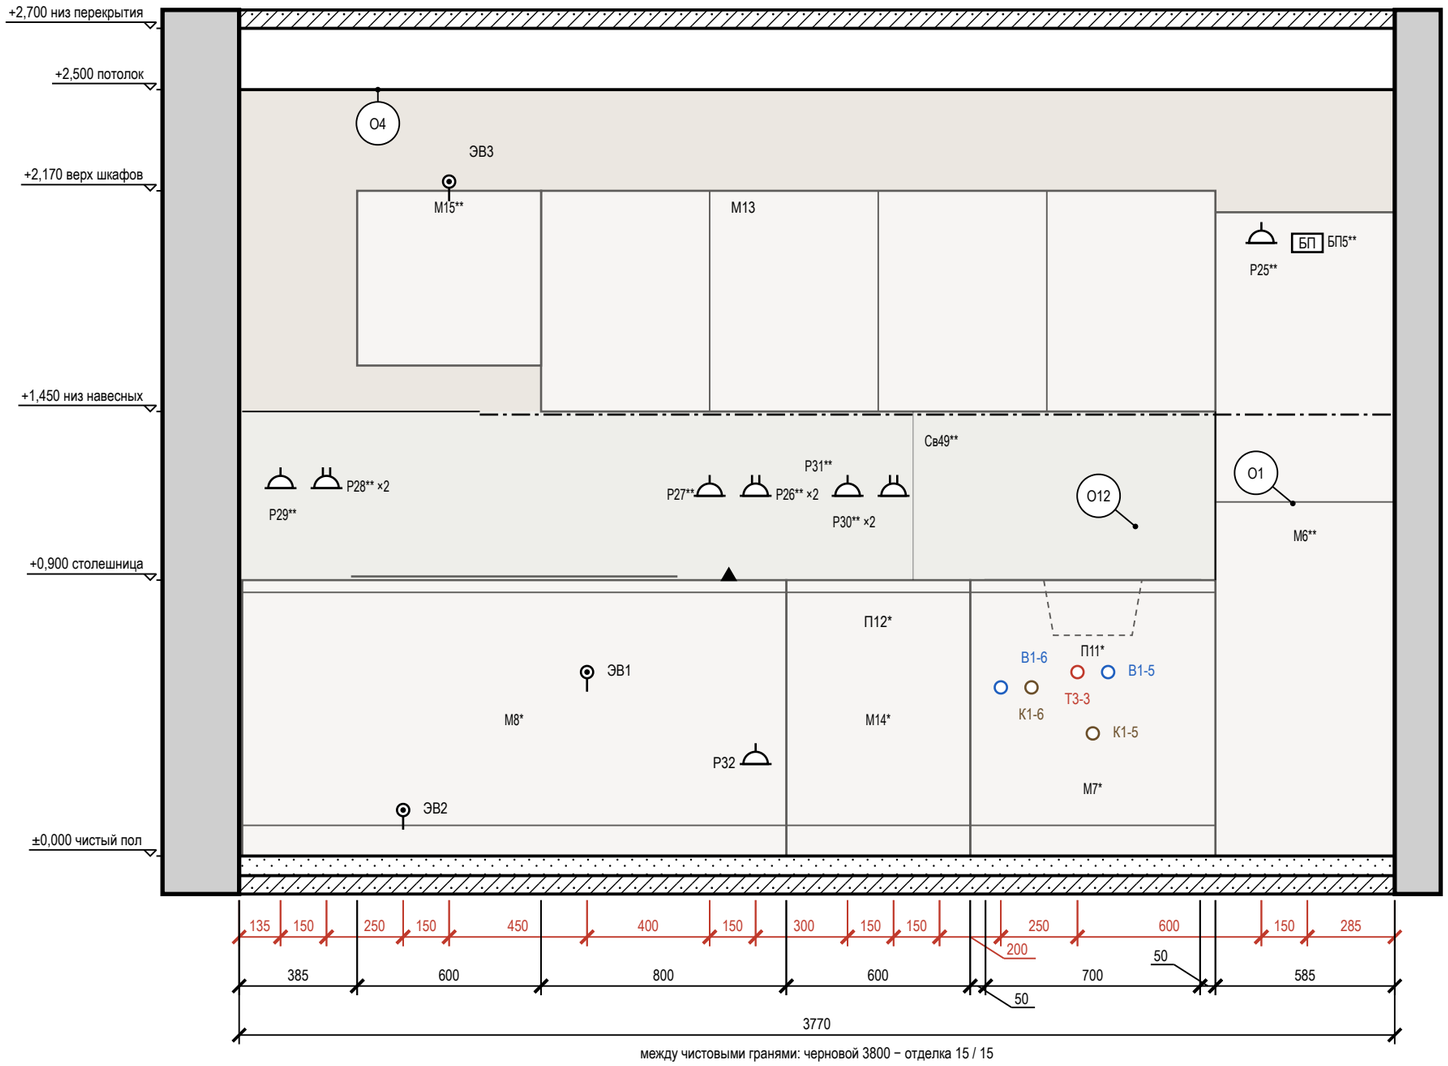

между чистовыми гранями: черновой 3800 − отделка 15 / 15

Ведомость точек и выводов

Марка	Что это	Гр.	Н, мм	От угла, мм	Примечание
Р29**	розетка: фартук	7	1200	135	
Р28**	розетка: фартук	7	1200	285	рамка 2 поста
ЭВ2	вывод кабеля: духовой шкаф	9	150	535	
ЭВ3	вывод кабеля: вытяжка — над корпусом	11	2200	685	
ЭВ1	вывод кабеля: варочная панель за ящиком	8	600	1135	
Р27**	розетка: фартук	7	1175	1535	
Р32	розетка: посудомоечная машина	10	300	1685	
Р26**	розетка: фартук	7	1175	1685	рамка 2 поста
Р31**	розетка: фартук между мойкой и варочной	7	1175	1985	
Р30**	розетка: фартук между мойкой и варочной	7	1175	2135	рамка 2 поста
Св49**	светильник настенный	2	1440	2285	лента 785–3785 от угла
В1-6	холодная вода — посудомоечная машина		550	2485	кран ПММ в шкафу мойки
К1-6	канализация — посудомоечная машина		550	2585	Ø40; слив ПММ в шкафу мойки
Т3-3	горячая вода — мойка кухонная		600	2735	межос. 100
К1-5	канализация — мойка кухонная		400	2785	Ø50
В1-5	холодная вода — мойка кухонная		600	2835	межос. 100
Р25**	розетка: холодильник — в своём модуле, над нишей, за съёмной панелью	11	2000	3335	
БП5**	блок питания LED: в пенале М6**, верх, съёмная панель	2	2000	3485	

Условные обозначения

- розетка с заземляющим контактом; у знака марка, ×N — постов в рамке, гр. — группа щита, Н — высота оси, мм
- вывод кабеля для подключения прибора (без розетки), марка ЭВ
- светодиодная лента в профиле / в карнизе короба
- БП — блок питания LED, с доступом (люк от 100×100 мм)
- вывод В1 (код — в ведомости привязок)
- вывод Т3 (код — в ведомости привязок)
- вывод К1 (код — в ведомости привязок)
- привязки точек и выводов от угла и от пола, мм
- мебель и приборы — фасад по расстановке (условно)
- стены и перекрытия в сечении
- плитка: сетка швов по формату, ▲ — ось старта
- окраска: тон — цвет по коду производителя (условно)
- О1 — марка отделки по реестру отделки альбома
- А — марка развёртки: буква стены, стрелка взгляд

Примечания

1. Развёртки — вид на стену изнутри помещения, по часовой стрелке; расположение — на листе 89; размеры — в мм по чистовым поверхностям; отметки — в м от ±0,000; высоты Н — от чистого пола помещения до оси изделия, у декора — до центра.
2. Красная цепочка — привязки электроточек и выводов по осям от угла чистовых стен; высота Н — у знака, от чистого пола до оси; высоты мебели, проёмов и границ отделки — колонкой отметок слева. У знака — короткая марка; назначение, группа щита, высота и привязка каждой точки и вывода — в «Ведомости точек и выводов» под видами (каждая точка — строка).
3. Отделка стен — по ведомости отделки помещений, лист 67.
4. У знака электроточки: марка (Р — розетка, S — выключатель, Св — светильник, ЭВ — вывод кабеля), ×N — число постов в рамке, гр. — группа щита, Н — высота оси от чистого пола, мм; группы по клавишам выключателя — на листе выключателей.
5. Схема мебели, приборов и декора не является технической документацией для производства мебели; габариты — по паспортам изделий (* — высота не задана в проекте, показана по типовому изделию).
6. Выводы кухонной техники — по утверждённому проекту кухни: привязки выводов даются от осей модулей гарнитура.
7. Потолок — у каждой стены свой, по плану потолков (ПТ1); ступени — зоной, кромка короба перед нишей — тонкой линией; в поле потолка: ПТ2 +2,600.

Допущения и предложения на листе. Знак «*» принято (замерить): отметка существующего пола. Знак «**» предложено (согласовать): дверь пом. 6 (стена В). См. лист открытых вопросов (листы 6–11).

1000 мм · печать 1:1

Изм.	Кол.уч	Лист	№ док.	Подп.	Дата
Разраб.		Кырлан А.С.			13.11.26
Пров.					
ГИП					
Н. контр.					
Утв.					

ГД-2026-003-АИ

Трёхкомнатная квартира

Общая площадь 78,95* м² · * размеры со скана, не замерены (реестр — л. 6–11, К-13)

Дизайн-проект интерьера трёхкомнатной квартиры

Стадия	Лист	Листов
РП	106	132

Развёртка стены В1. Кухня-гостиная (пом. 6), кухонный фронт

М 1:20

Кырлан Александр Сергеевич


выпуск 13.11.2026 № 6f3a8abb2c · стр. 115 из 157

Развёртка стены А. Кухня-гостиная (пом. 6)

Кухня-гостиная (пом. 6) · вид изнутри помещения · размеры в мм, отметки в м

ПРЕДВАРИТЕЛЬНО · не для производства работ · открыто пунктов: 28 (реестр — л. 6–11)

Стена А (М 1:25)

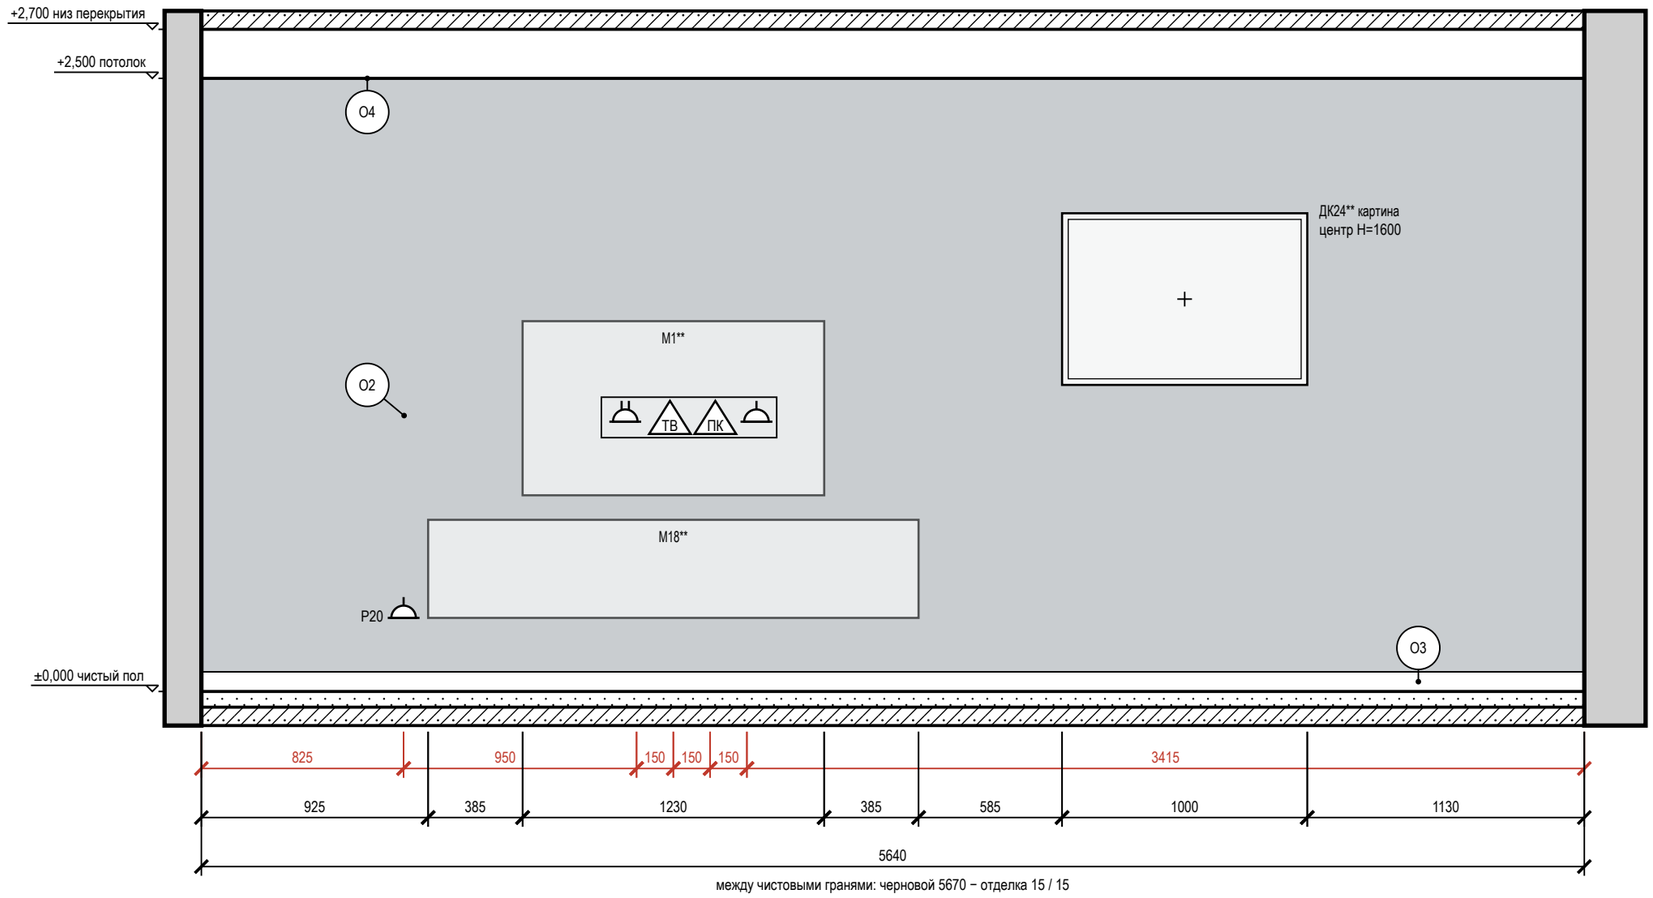


между чистовыми гранями: черновой 5670 − отделка 15 / 15

Условные обозначения

- розетка с заземляющим контактом; у знака — марка, ×N постов в рамке, гр. — группа щита, Н — высота оси, мм
- ПК — розетка компьютерная RJ45
- ТВ — розетка телевизионная
- привязки точек и выводов от угла и от пола, мм
- мебель и приборы — фасад по расстановке (условно)
- картина (декор): марка Д, крест — центр, Н — высота центра, мм
- стены и перекрытия в сечении
- окраска: тон — цвет по коду производителя (условно)
- О1 — марка отделки по реестру отделки альбома
- А — марка развёртки: буква стены, стрелка — взгляд

Схема развёрток (М 1:100)

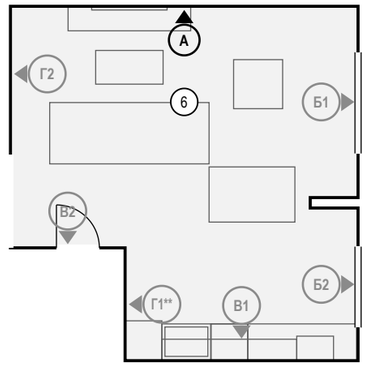

Ведомость точек и выводов

Марка	Что это	Гр.	Н, мм	От угла, мм	Примечание
Р20	розетка: у ТВ-тумбы	6	300	825	
Р18**	розетка: ТВ (в одной зоне с ТВ1, LAN3) — за экраном М1** на поворотном кронштейне, доступ при отведённом экране	6	1100	1775	рамка 2 поста
ТВ1	розетка ТВ: ТВ-зона — за экраном М1** на поворотном кронштейне, доступ при отведённом экране		1100	1925	

Марка	Что это	Гр.	Н, мм	От угла, мм	Примечание
LAN3	розетка RJ45: Smart TV — за экраном М1** на поворотном кронштейне, доступ при отведённом экране		1100	2075	
Р19**	розетка: ТВ-приставка (в одной зоне с ТВ1, LAN3) — за экраном М1** на поворотном кронштейне, доступ при отведённом экране	6	1100	2225	

Ведомость изделий и проёмов (на листе)

Марка	Изделие, проём	На виде Ш×В, мм	Низ, мм
М18**	тумба под ТВ подвесная, низ на 300 мм от пола	2000×400	300
М1**	телевизор на поворотном кронштейне, центр экрана на 1150 мм от пола	1230×710	800
ДК24**	картина	1000×700	1250

Примечания

1. Развёртки — вид на стену изнутри помещения, по часовой стрелке; расположение — на схеме листа и на листе 89; размеры — в мм по чистовым поверхностям; отметки — в м от ±0,000; высоты Н — от чистого пола помещения до оси изделия, у декора — до центра.
2. Красная цепочка — привязки электроточек и выводов по осям от угла чистовых стен; высота Н — у знака, от чистого пола до оси; высоты мебели, проёмов и границ отделки — колонкой отметок слева. У знака — короткая марка; назначение, группа щита, высота и привязка каждой точки и вывода — в «Ведомости точек и выводов» под видами (каждая точка — строка).
3. Отделка стен — по ведомости отделки помещений, лист 67.
4. У знака электроточки: марка (Р — розетка, S — выключатель, Св — светильник, ЭВ — вывод кабеля), ×N — число постов в рамке, гр. — группа щита, Н — высота оси от чистого пола, мм; группы по клавишам выключателя — на листе выключателей.
5. Схема мебели, приборов и декора не является технической документацией для производства мебели; габариты — по паспортам изделий.
6. Картины и зеркала крепить к основанию по паспорту изделия (закладные и анкеры — в перечне скрытых работ); крест — ось центра предмета.
7. Потолок — у каждой стены свой, по плану потолков (ПТ1); ступени — зоной, кромка короба перед нишей — тонкой линией; в поле потолка: ПТ2 +2,600.
8. Часть марок не уместилась у знаков: коды, высоты и привязки этих позиций — в ведомости точек и выводов под видами.

Допущения и предложения на листе. Знак «*» принято (замерить): отметка существующего пола. Знак «**» предложено (согласовать): дверь пом. 6 (стена В). См. лист открытых вопросов (листы 6–11).

1000 мм · печать 1:1

Изм.	Кол.уч	Лист	№ док.	Подп.	Дата
Разраб.		Кырлан А.С.			13.11.26
Пров.					
ГИП					
Н. контр.					
Утв.					

ГД-2026-003-АИ

Трёхкомнатная квартира

Общая площадь 78,95* м² · * размеры со скана, не замерены (реестр — л. 6–11, К-13)

Дизайн-проект интерьера трёхкомнатной квартиры

Стадия	Лист	Листов
РП	107	132

Развёртка стены А. Кухня-гостиная (пом. 6)

М 1:25

Кырлан Александр Сергеевич


выпуск 13.11.2026 № 6f3a8abb2c · стр. 116 из 157

Развёртки стен Б1, В2. Кухня-гостиная (пом. 6)

Кухня-гостиная (пом. 6) · вид изнутри помещения · размеры в мм, отметки в м


ПРЕДВАРИТЕЛЬНО · не для производства работ · открыто пунктов: 28 (реестр — л. 6–11)

Стена Б1 (М 1:25)

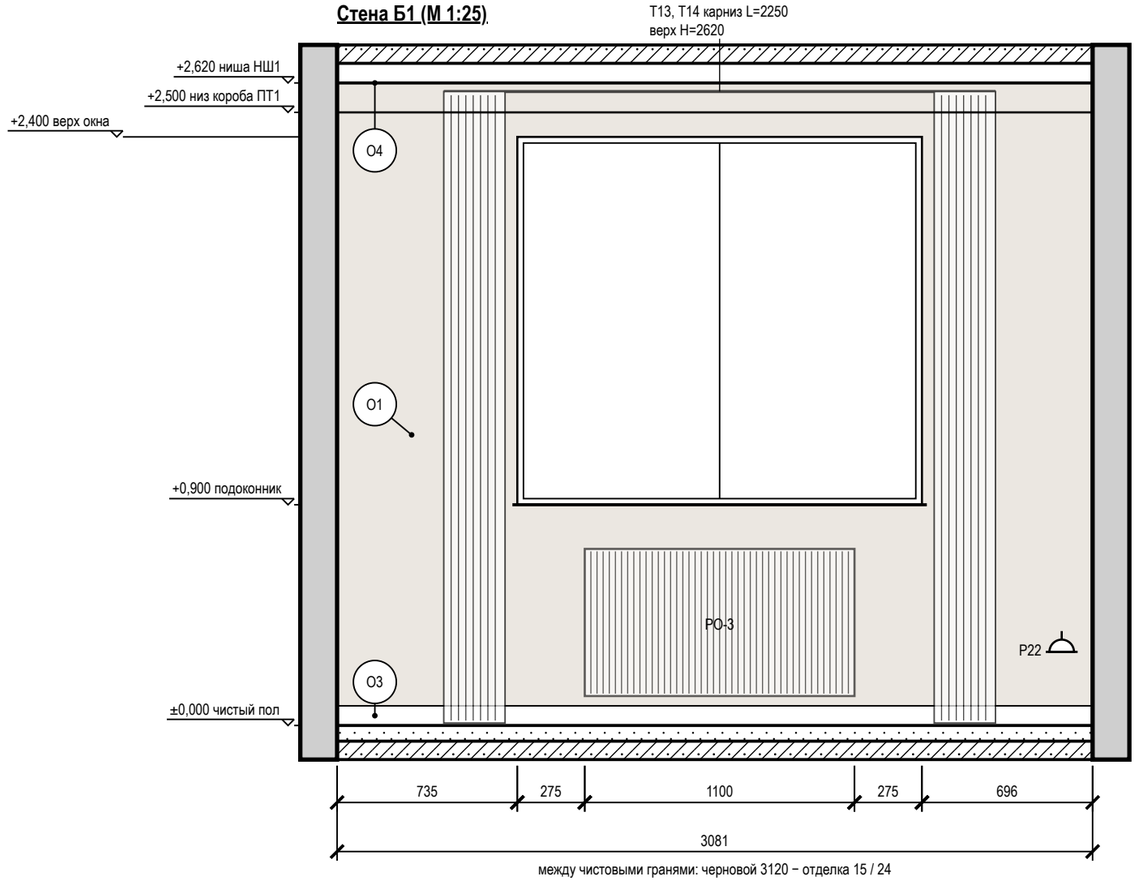

между чистовыми гранями: черновой 3120 − отделка 15 / 24

Стена В2 (М 1:25)

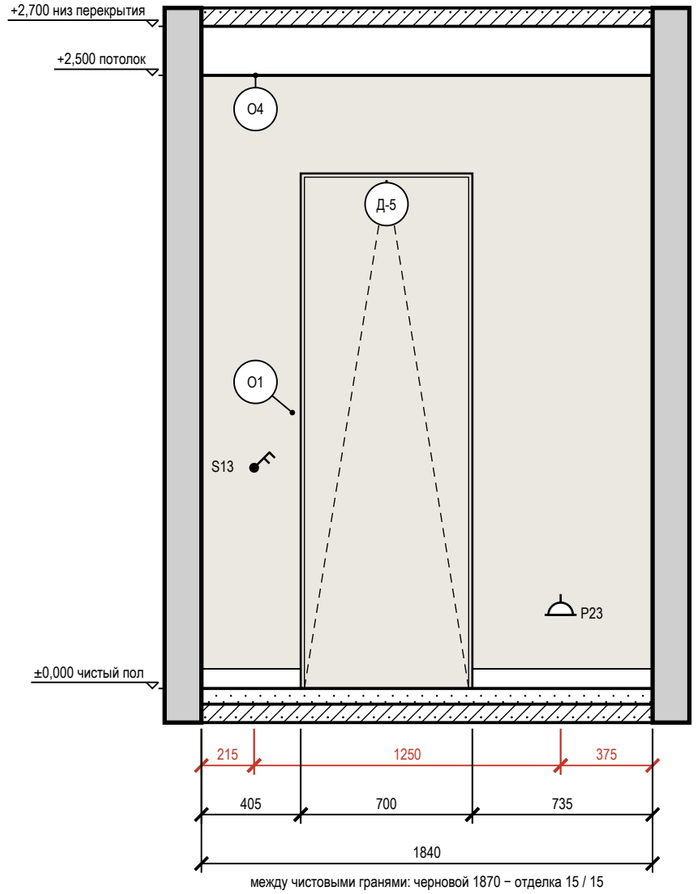


между чистовыми гранями: черновой 1870 − отделка 15 / 15

Условные обозначения

- розетка с заземляющим контактом; у знака марка, ×N — постов в рамке, гр. — группа щита, H — высота оси, мм
- выключатель одноклавишный
- выключатель двухклавишный (флажков — по числу клавиш)
- привязки точек и выводов от угла и от пола, мм
- мебель и приборы — фасад по расстановке (условно)
- карниз (шина) и шторы в собранном виде: марка T, длина L, верх H
- дверь скрытого монтажа: полотно в плоскости стены (узел — на листе узлов)
- окно: проём, рама, подоконник
- радиатор отопления; марка — по плану отопления
- стены и перекрытия в сечении
- окраска: тон — цвет по коду производителя (условно)
- О1 — марка отделки по реестру отделки альбома
- А — марка развёртки: буква стены, стрелка взгляд

Схема развёрток (М 1:100)

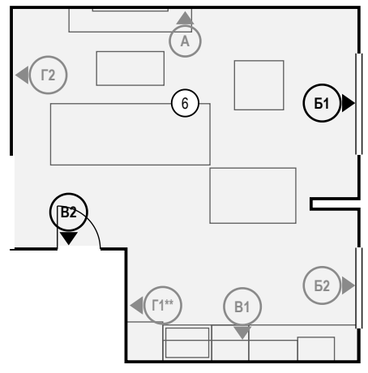

Ведомость точек и выводов

Стена	Марка	Что это	Гр.	H, мм	От угла, мм	Примечание
Б1	Р22	розетка: общего назначения	6	300	2955	
В2	S13	выключатель	3	900	215	

Стена	Марка	Что это	Гр.	H, мм	От угла, мм	Примечание
В2	Р23	розетка: уборка, пылесос	6	300	1465	

Примечания

1. Развёртки — вид на стену изнутри помещения, по часовой стрелке; расположение — на схеме листа и на листе 89; размеры — в мм по чистовым поверхностям; отметки — в м от ±0,000; высоты H — от чистого пола помещения до оси изделия, у декора — до центра.
2. Красная цепочка — привязки электроточек и выводов по осям от угла чистовых стен; высота H — у знака, от чистого пола до оси; высоты мебели, проёмов и границ отделки — колонкой отметок слева. У знака — короткая марка; назначение, группа щита, высота и привязка каждой точки и вывода — в «Ведомости точек и выводов» под видами (каждая точка — строка).
3. Отделка стен — по ведомости отделки помещений, лист 67.
4. У знака электроточки: марка (Р — розетка, S — выключатель, Св — светильник, ЭВ — вывод кабеля), ×N — число постов в рамке, гр. — группа щита, H — высота оси от чистого пола, мм; группы по клавишам выключателя — на листе выключателей.
5. Схема мебели, приборов и декора не является технической документацией для производства мебели; габариты — по паспортам изделий.
6. Карнизы (шины) — по ведомости текстиля декоратора: длина L и верх H на развёртке — те же числа, что в ведомости; крепление — до окраски потолка.
7. Двери скрытого монтажа — полотно в плоскости стены, отделка стены по полотну, плинтус прерывается у короба (узел — на листе узлов).
8. Потолок — у каждой стены свой, по плану потолков (НШ1, ПТ1); ступени — зоной, кромка короба перед нишей — тонкой линией; в поле потолка: ПТ2 +2,600.

Допущения и предложения на листе. Основа листа: размеры сняты со скана плана заказчика по размерным цепочкам, контрольный обмер на объекте не выполнялся (К-13); высота потолка 2700 мм принята: на плане заказчика не указана (К-11); толщины стен приняты: наружные 250 мм, перегородки 150 мм (на плане 85–190 мм) (К-13); разрешённая мощность 15 кВт принята по типовой квартире, технических условий нет (К-14); утолщение стены 190 × 1360 мм и элемент 1470 × 160 мм плана заказчика не определены (К-12); ниши санузла 2 закрыты перегородкой и фальш-стеной: проектное решение, на плане заказчика ниша у входа открыта (К-18); несущие стены не определены: до технического заключения все существующие стены считаются несущими (К-20); окна существующие и сохраняются; подоконная доска и глубина откосов не заданы — приняты, не замерены (К-27); подрайон климата не задан — принят не северный (жилые от 2,5 м) (К-29). Знак «*» — принято, не замерено (замерить): К-13: отметка существующего пола. Знак «**» — предложено, не утверждено (согласовать): К-9: Г1; К-25: дверь пом. 6 (стена В). См. лист открытых вопросов (лист 6, запись К-9; лист 7, записи К-11–К-14, К-18, К-20; лист 8, записи К-25, К-27, К-29).

1000 мм · печать 1:1

Изм.	Кол.уч	Лист	№ док.	Подп.	Дата
Разраб.		Кырлан А.С.			13.11.26
Пров.					
ГИП					
Н. контр.					
Утв.					

ГД-2026-003-АИ

Трёхкомнатная квартира

Общая площадь 78,95* м² · * размеры со скана, не замерены (реестр — л. 6–11, К-13)

Дизайн-проект интерьера трёхкомнатной квартиры

Стадия	Лист	Листов
РП	108	132

Развёртки стен Б1, В2. Кухня-гостиная (пом. 6)

М 1:25


Кырлан Александр Сергеевич

выпуск 13.11.2026 № 6f3a8abb2c · стр. 117 из 157

Развёртки стен Г1, Г2. Кухня-гостиная (пом. 6)


Кухня-гостиная (пом. 6) · вид изнутри помещения · размеры в мм, отметки в м

Стена Г1** (М 1:25)

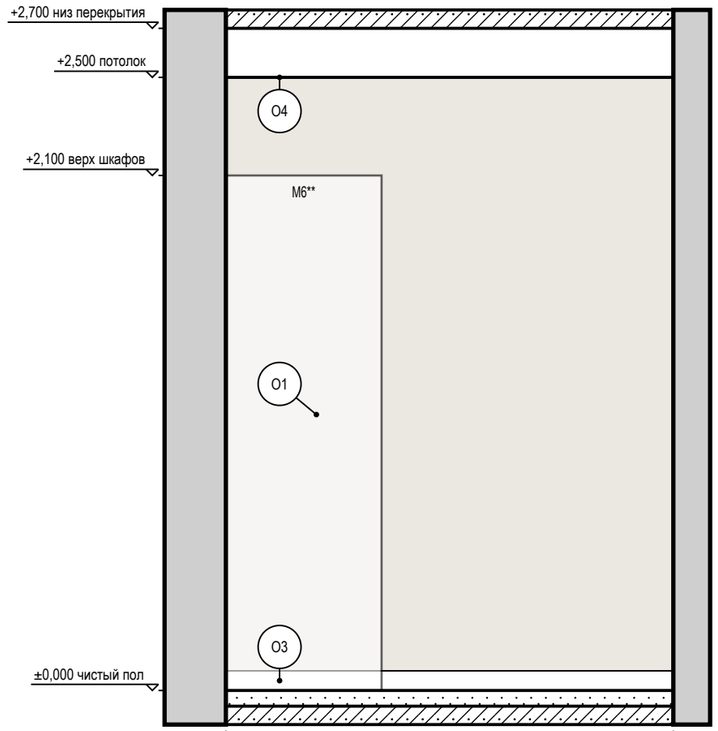

между чистовыми гранями: черновой 1840 − отделка 15 / 0

Стена Г2 (М 1:25)

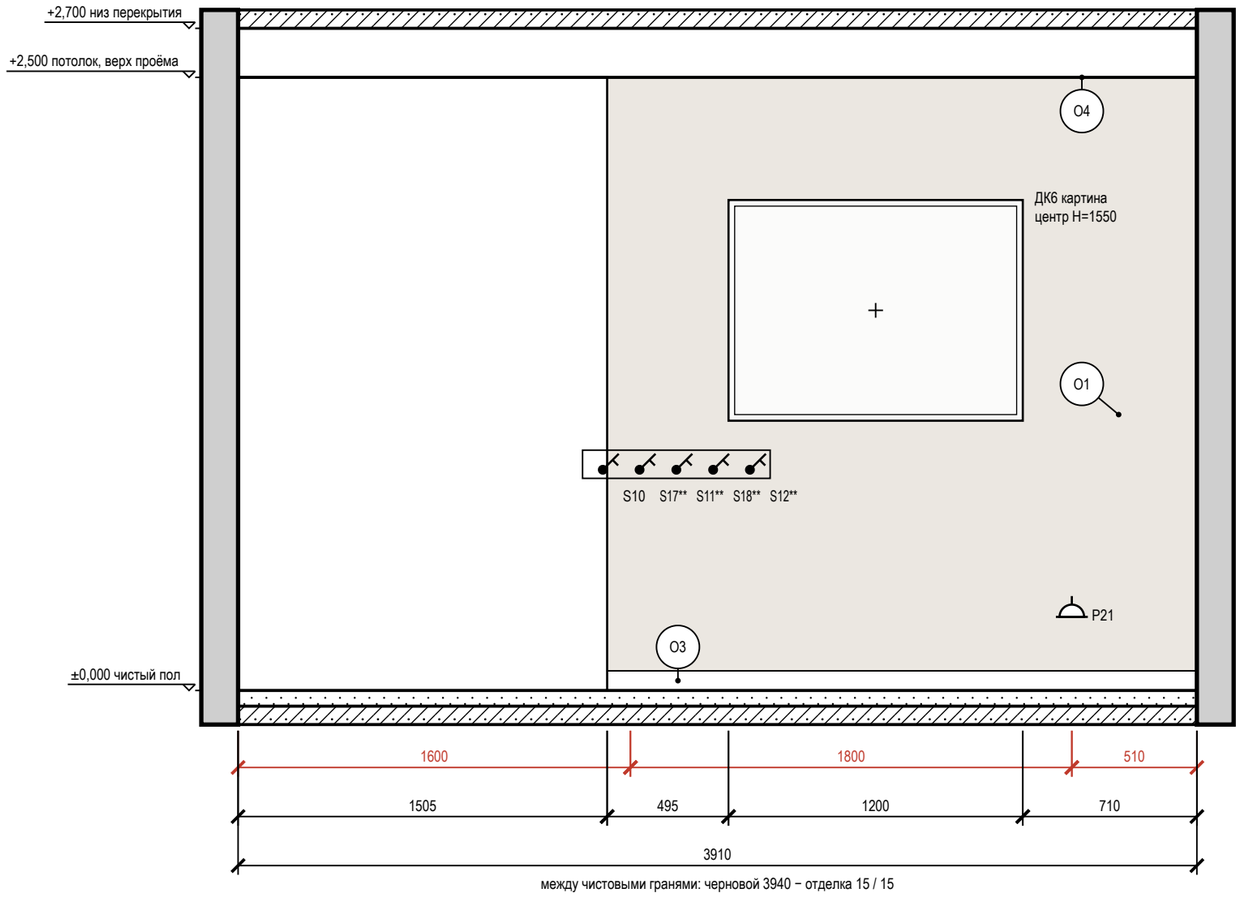

между чистовыми гранями: черновой 3940 − отделка 15 / 15


Ведомость точек и выводов

Стена	Марка	Что это	Гр.	Н, мм	От угла, мм	Примечание
Г2	S10	выключатель	2	900	1600	
Г2	S17**	выключатель	2	900	1680	
Г2	S11**	выключатель	2	900	1805	
Г2	S18**	выключатель	2	900	1885	
Г2	S12**	выключатель	2	900	1965	
Г2	Р21	розетка: торшер	6	300	3400	

Условные обозначения

- розетка с заземляющим контактом; у знака — марка, ×N постов в рамке, гр. — группа щита, Н — высота оси, мм
- выключатель одноклавишный
- привязки точек и выводов от угла и от пола, мм
- мебель и приборы — фасад по расстановке (условно)
- картина (декор): марка Д, крест — центр, Н — высота центра, мм
- дверной проём; марка двери — в кружке
- стены и перекрытия в сечении
- окраска: тон — цвет по коду производителя (условно)
- О1 — марка отделки по реестру отделки альбома
- А — марка развёртки: буква стены, стрелка — взгляд

Схема развёрток (М 1:200)

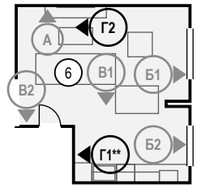

Примечания

1. Развёртки — вид на стену изнутри помещения, по часовой стрелке; расположение — на схеме листа и на листе 89; размеры — в мм по чистовым поверхностям; отметки — в м от ±0,000; высоты Н — от чистого пола помещения до оси изделия, у декора — до центра.
2. Красная цепочка — привязки электроточек и выводов по осям от угла чистовых стен; высота Н — у знака, от чистого пола до оси; высоты мебели, проёмов и границ отделки — колонкой отметок слева. У знака — короткая марка; назначение, группа щита, высота и привязка каждой точки и вывода — в «Ведомости точек и выводов» под видами (каждая точка — строка).
3. Отделка стен — по ведомости отделки помещений, лист 67.
4. У знака электроточки: марка (Р — розетка, S — выключатель, Св — светильник, ЭВ — вывод кабеля), ×N — число постов в рамке, гр. — группа щита, Н — высота оси от чистого пола, мм; группы по клавишам выключателя — на листе выключателей.
5. Схема мебели, приборов и декора не является технической документацией для производства мебели; габариты — по паспортам изделий.
6. Картины и зеркала крепить к основанию по паспорту изделия (закладные и анкеры — в перечне скрытых работ); крест — ось центра предмета.
7. Потолок — у каждой стены свой, по плану потолков (ПТ1); ступени — зоной, кромка короба перед нишей — тонкой линией; в поле потолка: ПТ2 +2,600.

Допущения и предложения на листе. Знак «*» принято (замерить): отметка существующего пола. Знак «**» предложено (согласовать): дверь пом. 6 (стена В). См. лист открытых вопросов (листы 6–11).

1000 мм · печать 1:1

Изм.	Кол.уч	Лист	№ док.	Подп.	Дата
Разраб.		Кырлан А.С.			13.11.26
Пров.					
ГИП					
Н. контр.					
Утв.					

ГД-2026-003-АИ

Трёхкомнатная квартира

Общая площадь 78,95* м² · * размеры со скана, не замерены (реестр — л. 6–11, К-13)

Дизайн-проект интерьера трёхкомнатной квартиры

Стадия	Лист	Листов
РП	109	132

Развёртки стен Г1, Г2. Кухня-гостиная (пом. 6)

М 1:25

Кырлан Александр Сергеевич


выпуск 13.11.2026 № 6f3a8abb2c · стр. 118 из 157

Развёртки стен А, Б. Санузел 2 (пом. 7)

Санузел 2 (пом. 7) · вид изнутри помещения · размеры в мм, отметки в м


ПРЕДВАРИТЕЛЬНО · не для производства работ · открыто пунктов: 28 (реестр — л. 6–11)

Стена А (М 1:25)

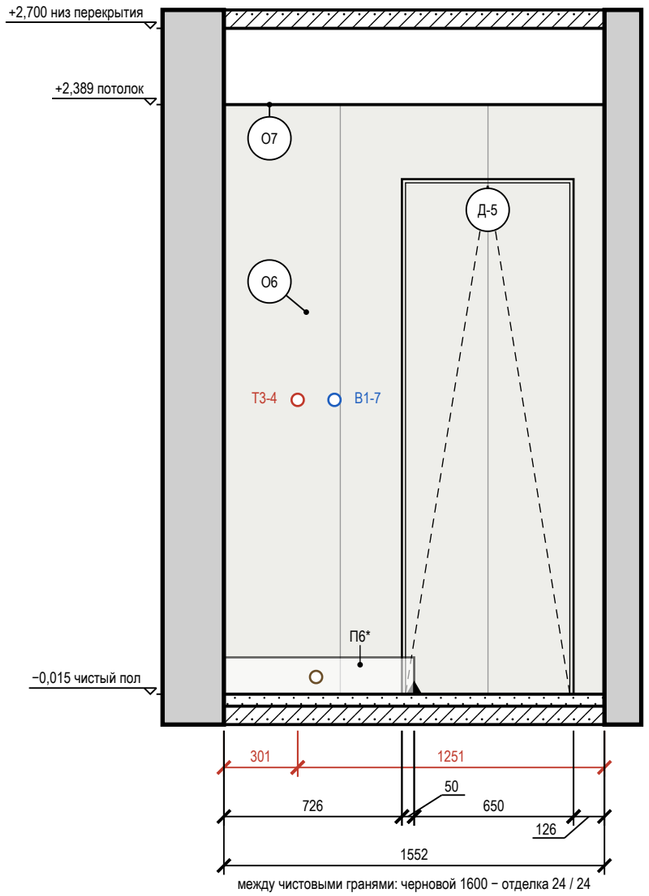

между чистовыми гранями: черновой 1600 − отделка 24 / 24

Стена Б (М 1:25)

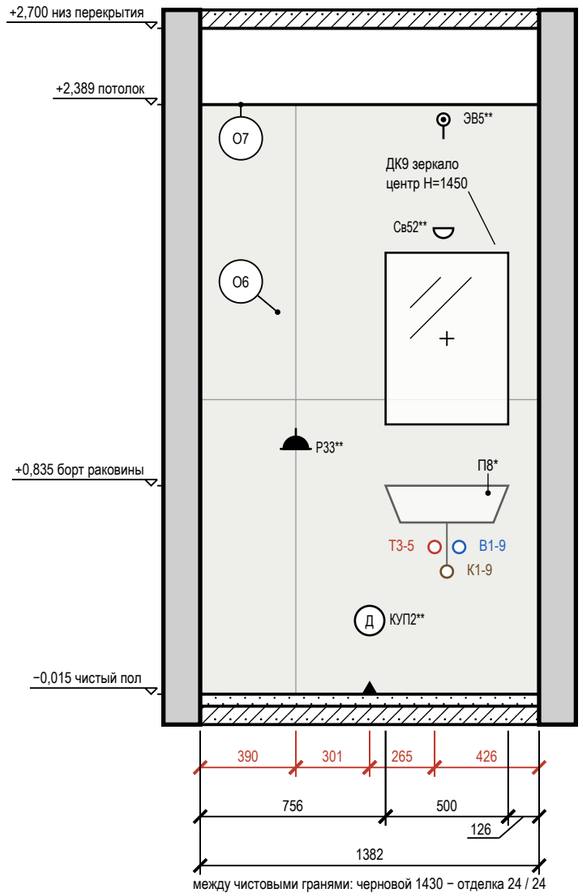

между чистовыми гранями: черновой 1430 − отделка 24 / 24

Ведомость точек и выводов

Стена	Марка	Что это	Гр.	Н, мм	От угла, мм	Примечание
А	Т3-4	горячая вода — душ		1200*	301	межос. 150
А	К1-7	канализация — душ		70*	376	Ø50; сифон поддона
А	В1-7	холодная вода — душ		1200*	451	межос. 150
Б	Р33**	розетка: фен у умывальника	13	1000	390	IP44
Б	КУП2**	КУП (уравнивание потенциалов): КУП уравнивание потенциалов (ДСУП)		300	691	
Б	Т3-5	горячая вода — умывальник		600*	956	межос. 100
Б	Св52**	светильник настенный	3	1900	992	
Б	ЭВ5**	вывод кабеля: вентилятор ВР3 (таймер выбега)	3	2343	992	
Б	К1-9	канализация — умывальник		500*	1006	Ø50
Б	В1-9	холодная вода — умывальник		600*	1056	межос. 100

Условные обозначения

- розетка влагозащищённая IP44
- вывод кабеля для подключения прибора (без розетки), марка ЭВ
- светильник настенный (бра), Н — высота оси
- вывод В1 (код — в ведомости привязок)
- вывод Т3 (код — в ведомости привязок)
- вывод К1 (код — в ведомости привязок)
- привязки точек и выводов от угла и от пола, мм
- мебель и приборы — фасад по расстановке (условно)
- зеркало: марка Д, крест — центр, Н — высота центра, мм
- дверь скрытого монтажа: полотно в плоскости стены (узел — на листе узлов)
- стены и перекрытия в сечении
- плитка: сетка швов по формату, ▲ — ось старта
- О1 — марка отделки по реестру отделки альбома
- А — марка развёртки: буква стены, стрелка взгляд

Ведомость отделки (на листе)

Марка	Поверхность	Материал, изделие	Цвет, код	Кол.
О6	стены	облицовка плиткой, 600×1200×9 мм, аналог: керамогранит под травертин, матовый, затирка CG2WA		5,6 м²
О7	потолок	окраска, Tikkurila Luja 7, матовая, подготовка Q3	Tikkurila V503 «Winter»	2,3 м²

Примечания

1. Развёртки — вид на стену изнутри помещения, по часовой стрелке; расположение — на листе 89; размеры — в мм по чистовым поверхностям; отметки — в м от ±0,000; высоты Н — от чистого пола помещения до оси изделия, у декора — до центра.
2. Красная цепочка — привязки электроточек и выводов по осям от угла чистовых стен; высота Н — у знака, от чистого пола до оси; высоты мебели, проёмов и границ отделки — колонкой отметок слева. У знака — короткая марка; назначение, группа щита, высота и привязка каждой точки и вывода — в «Ведомости точек и выводов» под видами (каждая точка — строка).
3. У знака электроточки: марка (Р — розетка, S — выключатель, Св — светильник, ЭВ — вывод кабеля), ×N — число постов в рамке, гр. — группа щита, Н — высота оси от чистого пола, мм; группы по клавишам выключателя — на листе выключателей.
4. Схема мебели, приборов и декора не является технической документацией для производства мебели; габариты — по паспортам изделий (* — высота не задана в проекте, показана по типовому изделию).
5. Выводы ВК — коды и высоты по листу выводов сантехники; * — высота принята по типовой практике монтажа, окончательно — по паспорту прибора.
6. Облицовка — по сетке швов 2 мм, раскладка от оси стены (треугольник у пола), целые ряды от пола; подрезки — по листу раскладки плитки.
7. Гидроизоляция в 2 слоя, заход на стены 200 мм; у душа — до 2000 и 500 мм за поддон — до облицовки, с актом скрытых работ и тестом проливом (узел — на листе узлов).
8. Картины и зеркала крепить к основанию по паспорту изделия (закладные и анкеры — в перечне скрытых работ); крест — ось центра предмета.
9. Двери скрытого монтажа — полотно в плоскости стены, отделка стены по полотну, плинтус прерывается у короба (узел — на листе узлов).
10. Часть марок не уместилась у знаков: коды, высоты и привязки этих позиций — в ведомости точек и выводов под видами.

Допущения и предложения на листе

Основа листа: размеры сняты со скана плана заказчика по размерным цепочкам, контрольный обмер на объекте не выполнялся (К-13); высота потолка 2700 мм принята: на плане заказчика не указана (К-11); толщины стен приняты: наружные 250 мм, перегородки 150 мм (на плане 85–190 мм) (К-13); разрешённая мощность 15 кВт принята по типовой квартире, технических условий нет (К-14); утолщение стены 190 × 1360 мм и элемент 1470 × 160 мм плана заказчика не определены (К-12); ниши санузла 2 закрыты перегородкой и фальш-стеной: проектное решение, на плане заказчика ниша у входа открыта (К-18); несущие стены не определены: до технического заключения все существующие стены считаются несущими (К-20); окна существующие и сохраняются; подоконная доска и глубина откосов не заданы — приняты, не замерены (К-27); подрайон климата не задан — принят не северный (жилые от 2,5 м) (К-29).

Знак «*» — принято, не замерено и не подтверждено (замерить на объекте): К-13: отметка существующего пола — отметка существующего пола и верха плиты не замерена: на плане заказчика отметок нет; нивелировка — в задании на обмер (К-13).

Знак «**» — предложение проектировщика, заказчиком не утверждено (согласовать с заказчиком): Св52 — Сдвиг под раскладку плитки стены Б на 14 мм вдоль стены — ось на шве или в центре плитки, привязка по таблице листа; ИЗ-4, ИЗ-9, К-7: Р33; ИЗ-8: ЭВ5 — Сдвиг под раскладку плитки стены Б на 114 мм вдоль стены и на 46 мм ниже — ось на шве или в центре плитки, привязка по таблице листа; КУП2 — коробка уравнивания потенциалов, проводник от шины PE.

См. лист открытых вопросов (лист 6, запись К-7; лист 7, записи К-11–К-14, К-18, К-20; лист 8, записи К-27, К-29; лист 9, записи ИЗ-4, ИЗ-8, ИЗ-9).

1000 мм · печать 1:1

Изм.	Кол.уч	Лист	№ док.	Подп.	Дата
Разраб.		Кырлан А.С.			13.11.26
Пров.					
ГИП					
Н. контр.					
Утв.					

ГД-2026-003-АИ

Трёхкомнатная квартира

Общая площадь 78,95* м² · * размеры со скана, не замерены (реестр — л. 6–11, К-13)

Дизайн-проект интерьера трёхкомнатной квартиры

Стадия	Лист	Листов
РП	110	132

Развёртки стен А, Б. Санузел 2 (пом. 7)

М 1:25

Кырлан Александр Сергеевич


выпуск 13.11.2026 № 6f3a8abb2c · стр. 119 из 157

Развёртки стен В, Г. Санузел 2 (пом. 7)

Санузел 2 (пом. 7) · вид изнутри помещения · размеры в мм, отметки в м


ПРЕДВАРИТЕЛЬНО · не для производства работ · открыто пунктов: 28 (реестр — л. 6–11)

Стена В (М 1:20)

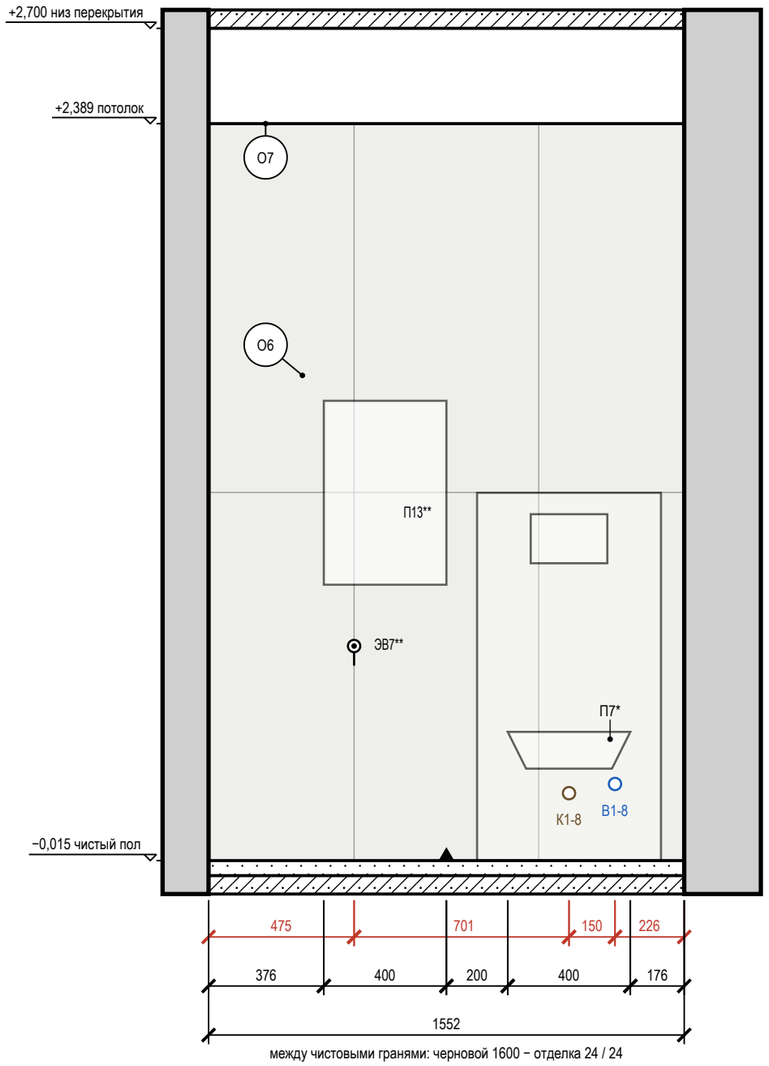

между чистовыми гранями: черновой 1600 − отделка 24 / 24

Стена Г (М 1:20)

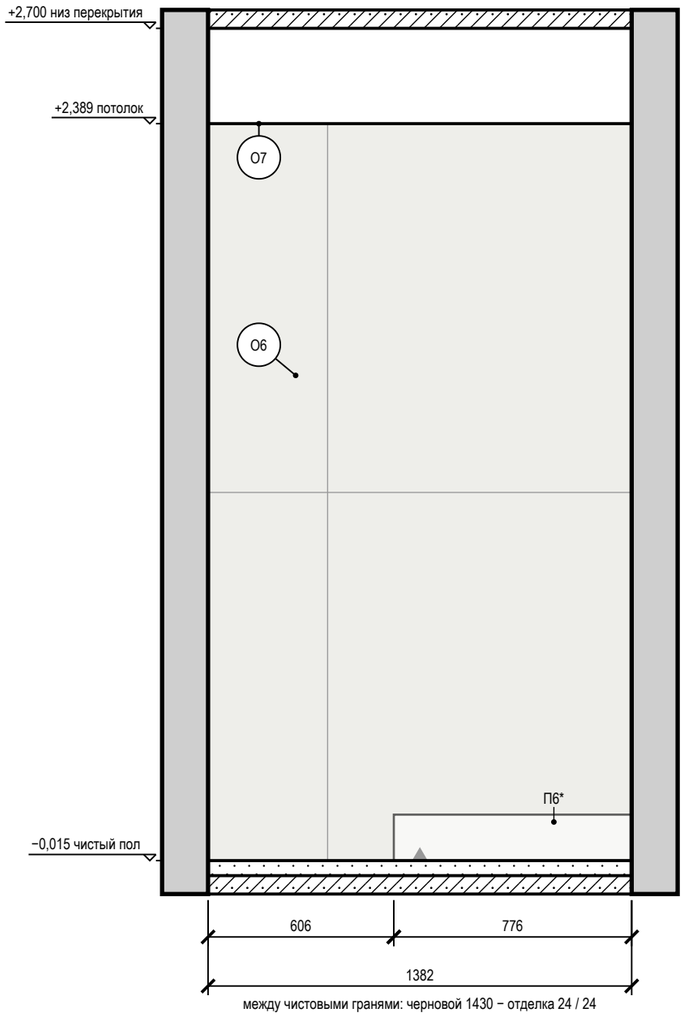

между чистовыми гранями: черновой 1430 − отделка 24 / 24

Ведомость точек и выводов

Стена	Марка	Что это	Гр.	Н, мм	От угла, мм	Примечание
В	ЭВ7**	вывод кабеля: полотенцесушитель П13**	13	700	475	
В	К1-8	канализация — унитаз подвесной		220*	1176	Ø110
В	В1-8	холодная вода — унитаз подвесной		250*	1326	в раме инсталляции


Условные обозначения

- вывод кабеля для подключения прибора (без розетки), марка ЭВ
- вывод В1 (код — в ведомости привязок)
- вывод К1 (код — в ведомости привязок)
- привязки точек и выводов от угла и от пола, мм
- мебель и приборы — фасад по расстановке (условно)
- стены и перекрытия в сечении
- плитка: сетка швов по формату, ▲ — ось старта
- О1 — марка отделки по реестру отделки альбома
- А — марка развёртки: буква стены, стрелка — взгляд

Ведомость отделки (на листе)

Марка	Поверхность	Материал, изделие	Цвет, код	Кол.
О6	стены	облицовка плиткой, 600×1200×9 мм, аналог: керамогранит под травертин, матовый, затирка CG2WA		7,1 м²
О7	потолок	окраска, Tikkurila Luja 7, матовая, подготовка Q3	Tikkurila V503 «Winter»	2,3 м²

Схема развёрток (М 1:50)

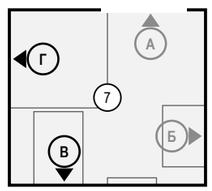

Примечания

1. Развёртки — вид на стену изнутри помещения, по часовой стрелке; расположение — на схеме листа и на листе 89; размеры — в мм по чистовым поверхностям; отметки — в м от ±0,000; высоты Н — от чистого пола помещения до оси изделия, у декора — до центра.
2. Красная цепочка — привязки электроточек и выводов по осям от угла чистовых стен; высота Н — у знака, от чистого пола до оси; высоты мебели, проёмов и границ отделки — колонкой отметок слева. У знака — короткая марка; назначение, группа щита, высота и привязка каждой точки и вывода — в «Ведомости точек и выводов» под видами (каждая точка — строка).
3. У знака электроточки: марка (Р — розетка, S — выключатель, Св — светильник, ЭВ — вывод кабеля), ×N — число постов в рамке, гр. — группа щита, Н — высота оси от чистого пола, мм; группы по клавишам выключателя — на листе выключателей.
4. Схема мебели, приборов и декора не является технической документацией для производства мебели; габариты — по паспортам изделий (* — высота не задана в проекте, показана по типовому изделию).
5. Выводы ВК — коды и высоты по листу выводов сантехники; * — высота принята по типовой практике монтажа, окончательно — по паспорту прибора.
6. Облицовка — по сетке швов 2 мм, раскладка от оси стены (треугольник у пола), целые ряды от пола; подрезки — по листу раскладки плитки.
7. Гидроизоляция в 2 слоя, заход на стены 200 мм; у душа — до 2000 и 500 мм за поддон — до облицовки, с актом скрытых работ и тестом проливом (узел — на листе узлов).

Допущения и предложения на листе. Основа листа: размеры сняты со скана плана заказчика по размерным цепочкам, контрольный обмер на объекте не выполнялся (К-13); высота потолка 2700 мм принята: на плане заказчика не указана (К-11); толщины стен приняты: наружные 250 мм, перегородки 150 мм (на плане 85–190 мм) (К-13); разрешённая мощность 15 кВт принята по типовой квартире, технических условий нет (К-14); утолщение стены 190 × 1360 мм и элемент 1470 × 160 мм плана заказчика не определены (К-12); ниши санузла 2 закрыты перегородкой и фальш-стеной: проектное решение, на плане заказчика ниша у входа открыта (К-18); несущие стены не определены: до технического заключения все существующие стены считаются несущими (К-20); окна существующие и сохраняются; подоконная доска и глубина откосов не заданы — приняты, не замерены (К-27); подрайон климата не задан — принят не северный (жилые от 2,5 м) (К-29). Знак «*» — принято, не замерено (замерить): К-13: отметка существующего пола. Знак «**» — предложено, не утверждено (согласовать): ИЗ-1: ЭВ7. См. лист открытых вопросов (лист 7, записи К-11–К-14, К-18, К-20; лист 8, записи К-27, К-29; лист 9, запись ИЗ-1).

1000 мм · печать 1:1

Изм.	Кол.уч	Лист	№ док.	Подп.	Дата
Разраб.		Кырлан А.С.			13.11.26
Пров.					
ГИП					
Н. контр.					
Утв.					

ГД-2026-003-АИ

Трёхкомнатная квартира

Общая площадь 78,95* м² · * размеры со скана, не замерены (реестр — л. 6–11, К-13)

Дизайн-проект интерьера трёхкомнатной квартиры

Стадия	Лист	Листов
РП	111	132

Развёртки стен В, Г. Санузел 2 (пом. 7)

М 1:20

Кырлан Александр Сергеевич


выпуск 13.11.2026 № 6f3a8abb2c · стр. 120 из 157

Развёртки стен А, Б. Коридор (пом. 8)

Коридор (пом. 8) · вид изнутри помещения · размеры в мм, отметки в м


ПРЕДВАРИТЕЛЬНО · не для производства работ · открыто пунктов: 28 (реестр — л. 6–11)

Стена А (М 1:25)

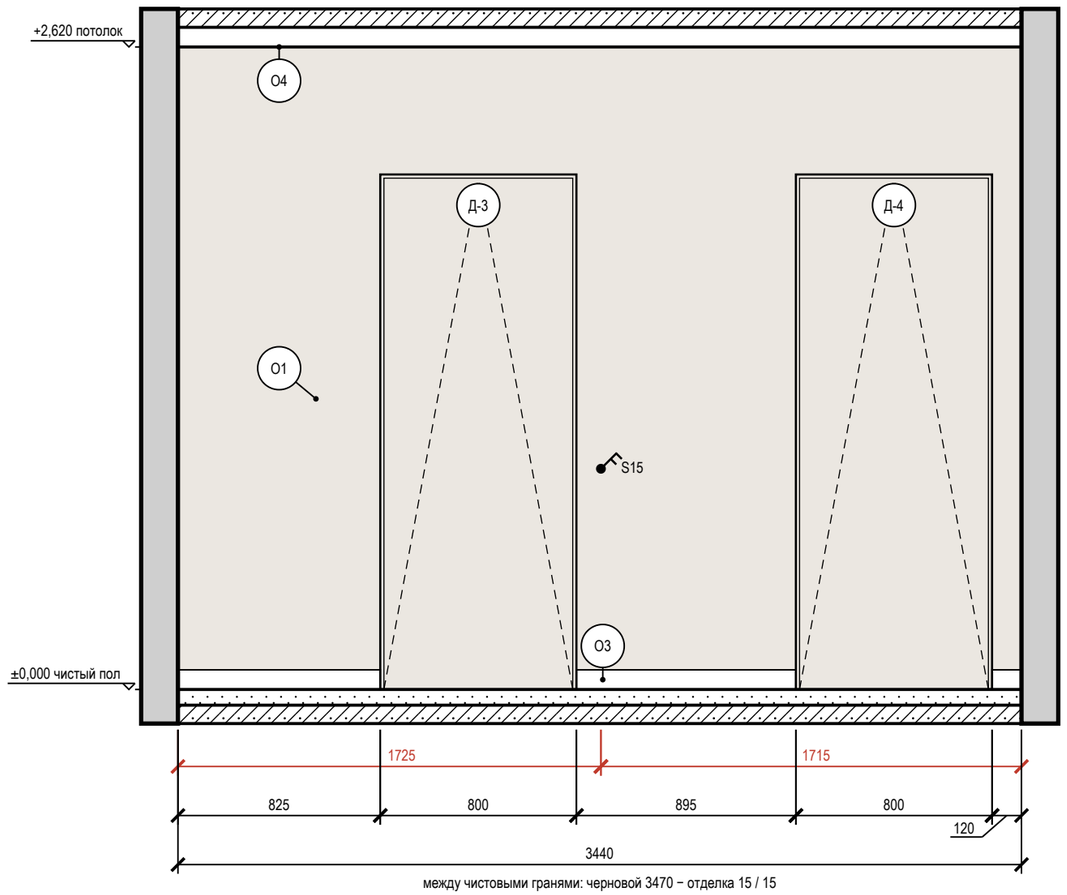

между чистовыми гранями: черновой 3470 − отделка 15 / 15

Стена Б (М 1:25)

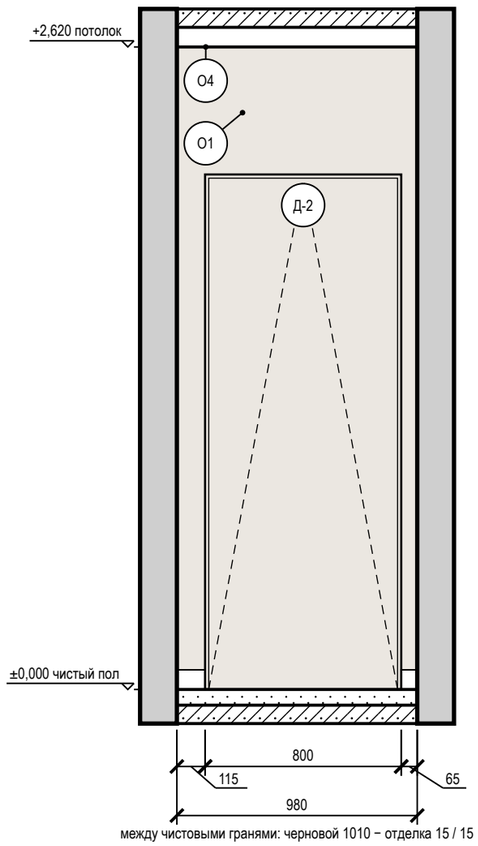

между чистовыми гранями: черновой 1010 − отделка 15 / 15


Условные обозначения

- выключатель одноклавишный
- выключатель двухклавишный (флажков — по числу клавиш)
- привязки точек и выводов от угла и от пола, мм
- мебель и приборы — фасад по расстановке (условно)
- дверь скрытого монтажа: полотно в плоскости стены (узел — на листе узлов)
- стены и перекрытия в сечении
- окраска: тон — цвет по коду производителя (условно)
- О1 — марка отделки по реестру отделки альбома
- А — марка развёртки: буква стены, стрелка — взгляд

Ведомость отделки (на листе)

Марка	Поверхность	Материал, изделие	Цвет, код	Кол.
О1	стены	окраска, Farrow & Ball Modern Emulsion, матовая, подготовка Q3	Farrow & Ball No. 241 «Skimming Stone»	6,5 м²
О3	плинтус	плинтус МДФ, h 80 мм, аналог: плинтус МДФ под покраску 80×16	Farrow & Ball No. 241 «Skimming Stone»	2 м
О4	потолок	окраска, Tikkurila Anti-Reflex 2, глубокоматовая, подготовка Q3	Tikkurila V503 «Winter»	3,5 м²

Схема развёрток (М 1:50)

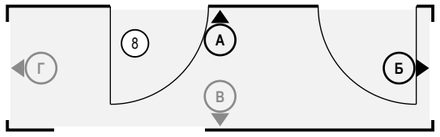

Ведомость точек и выводов

Стена	Марка	Что это	Гр.	Н, мм	От угла, мм	Примечание
А	S15	выключатель	3	900	1725	

Ведомость изделий и проёмов (на листе)

Стена	Марка	Изделие, проём	На виде Ш×В, мм	Низ, мм
А	Д-3	дверь скрытого монтажа	800×2100	0
А	Д-4	дверь скрытого монтажа	800×2100	0
Б	Д-2	дверь скрытого монтажа	800×2100	0

Примечания

1. Развёртки — вид на стену изнутри помещения, по часовой стрелке; расположение — на схеме листа и на листе 89; размеры — в мм по чистовым поверхностям; отметки — в м от ±0,000; высоты Н — от чистого пола помещения до оси изделия, у декора — до центра.
2. Красная цепочка — привязки электроточек и выводов по осям от угла чистовых стен; высота Н — у знака, от чистого пола до оси; высоты мебели, проёмов и границ отделки — колонкой отметок слева. У знака — короткая марка; назначение, группа щита, высота и привязка каждой точки и вывода — в «Ведомости точек и выводов» под видами (каждая точка — строка).
3. У знака электроточки: марка (Р — розетка, S — выключатель, Св — светильник, ЭВ — вывод кабеля), ×N — число постов в рамке, гр. — группа щита, Н — высота оси от чистого пола, мм; группы по клавишам выключателя — на листе выключателей.
4. Схема мебели, приборов и декора не является технической документацией для производства мебели; габариты — по паспортам изделий.
5. Двери скрытого монтажа — полотно в плоскости стены, отделка стены по полотну, плинтус прерывается у короба (узел — на листе узлов).

Допущения и предложения на листе. Основа листа: размеры сняты со скана плана заказчика по размерным цепочкам, контрольный обмер на объекте не выполнялся (К-13); высота потолка 2700 мм принята: на плане заказчика не указана (К-11); толщины стен приняты: наружные 250 мм, перегородки 150 мм (на плане 85–190 мм) (К-13); разрешённая мощность 15 кВт принята по типовой квартире, технических условий нет (К-14); утолщение стены 190 × 1360 мм и элемент 1470 × 160 мм плана заказчика не определены (К-12); ниши санузла 2 закрыты перегородкой и фальш-стеной: проектное решение, на плане заказчика ниша у входа открыта (К-18); несущие стены не определены: до технического заключения все существующие стены считаются несущими (К-20); окна существующие и сохраняются; подоконная доска и глубина откосов не заданы — приняты, не замерены (К-27); подрайон климата не задан — принят не северный (жилые от 2,5 м) (К-29). Знак «*» — принято, не замерено и не подтверждено (замерить на объекте): К-13: отметка существующего пола — отметка существующего пола и верха плиты не замерена: на плане заказчика отметок нет; нивелировка — в задании на обмер (К-13); К-25: дверь пом. 8 (стена А) — толщина стены в проёме принята 150 мм (как у всех перегородок модели), по скану плана заказчика стена 85 мм — не замерено (К-25); проём существующий, скрытый блок ставится в него с зазором 10–15 мм на сторону, полотно уже проёма; узел скрытой двери выполнен для принятой толщины 150 мм. См. лист открытых вопросов (лист 7, записи К-11–К-14, К-18, К-20; лист 8, записи К-25, К-27, К-29).

1000 мм · печать 1:1

Изм.	Кол.уч	Лист	№ док.	Подп.	Дата
Разраб.		Кырлан А.С.			13.11.26
Пров.					
ГИП					
Н. контр.					
Утв.					

ГД-2026-003-АИ

Трёхкомнатная квартира

Общая площадь 78,95* м² · * размеры со скана, не замерены (реестр — л. 6–11, К-13)

Дизайн-проект интерьера трёхкомнатной квартиры

Стадия	Лист	Листов
РП	112	132

Развёртки стен А, Б. Коридор (пом. 8)

М 1:25

Кырлан Александр Сергеевич


выпуск 13.11.2026 № 6f3a8abb2c · стр. 121 из 157

Развёртки стен В, Г. Коридор (пом. 8)

Коридор (пом. 8) · вид изнутри помещения · размеры в мм, отметки в м


ПРЕДВАРИТЕЛЬНО · не для производства работ · открыто пунктов: 28 (реестр — л. 6–11)

Стена В (М 1:25)

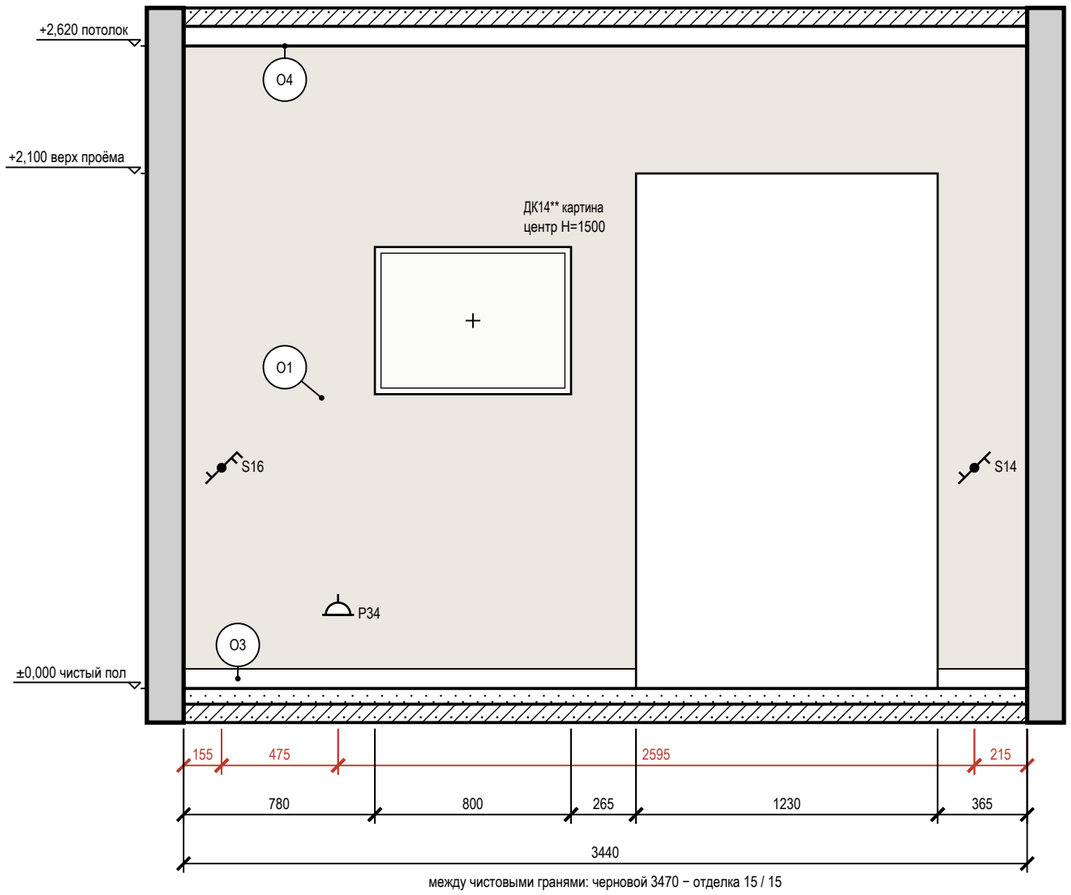

между чистовыми гранями: черновой 3470 − отделка 15 / 15

Стена Г (М 1:25)

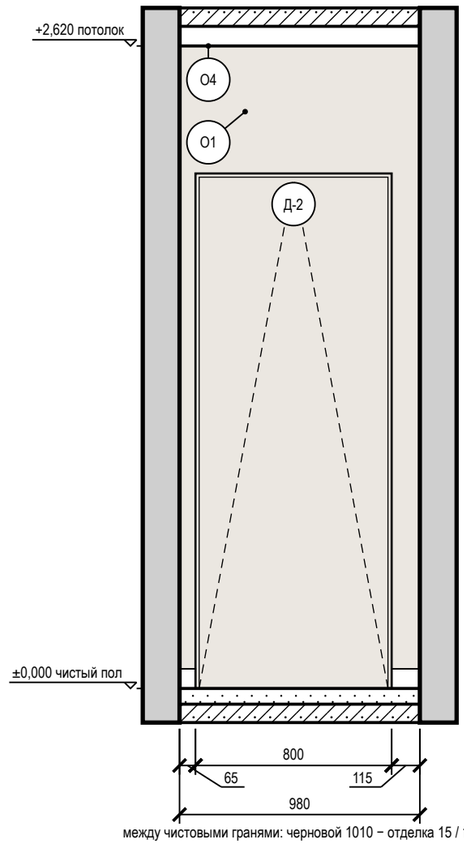

между чистовыми гранями: черновой 1010 − отделка 15 / 15

Условные обозначения

- розетка с заземляющим контактом; у знака — марка, ×N постов в рамке, гр. — группа щита, Н — высота оси, мм
- выключатель одноклавишный
- выключатель двухклавишный (флажков — по числу клавиш)
- выключатель с проходной или перекрёстной клавишей (обратный флажок); тип клавиши — в подписи
- привязки точек и выводов от угла и от пола, мм
- мебель и приборы — фасад по расстановке (условно)
- картина (декор): марка Д, крест — центр, Н — высота центра, мм
- дверь скрытого монтажа: полотно в плоскости стены (узел — на листе узлов)
- дверной проём; марка двери — в кружке
- стены и перекрытия в сечении
- окраска: тон — цвет по коду производителя (условно)
- О1 — марка отделки по реестру отделки альбома
- А — марка развёртки: буква стены, стрелка — взгляд

Ведомость отделки (на листе)

Марка	Поверхность	Материал, изделие	Цвет, код	Кол.
О1	стены	окраска, Farrow & Ball Modern Emulsion, матовая, подготовка Q3	Farrow & Ball No. 241 «Skimming Stone»	7,3 м²
О3	плинтус	плинтус МДФ, h 80 мм, аналог: плинтус МДФ под покраску 80×16	Farrow & Ball No. 241 «Skimming Stone»	2,4 м
О4	потолок	окраска, Tikkurila Anti-Reflex 2, глубокоматовая, подготовка Q3	Tikkurila V503 «Winter»	3,5 м²


Ведомость точек и выводов

Стена	Марка	Что это	Гр.	Н, мм	От угла, мм	Примечание
В	S16	выключатель	1	900	155	
В	Р34	розетка: уборка	6	300	630	
В	S14	выключатель	2	900	3225	

Ведомость изделий и проёмов (на листе)

Стена	Марка	Изделие, проём	На виде Ш×В, мм	Низ, мм
В	ДК14**	картина	800×600	1200
Г	Д-2	дверь скрытого монтажа	800×2100	0

Схема развёрток (М 1:50)

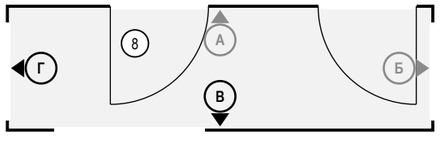

Примечания

1. Развёртки — вид на стену изнутри помещения, по часовой стрелке; расположение — на схеме листа и на листе 89; размеры — в мм по чистовым поверхностям; отметки — в м от ±0,000; высоты Н — от чистого пола помещения до оси изделия, у декора — до центра.
2. Красная цепочка — привязки электроточек и выводов по осям от угла чистовых стен; высота Н — у знака, от чистого пола до оси; высоты мебели, проёмов и границ отделки — колонкой отметок слева. У знака — короткая марка; назначение, группа щита, высота и привязка каждой точки и вывода — в «Ведомости точек и выводов» под видами (каждая точка — строка).
3. У знака электроточки: марка (Р — розетка, S — выключатель, Св — светильник, ЭВ — вывод кабеля), ×N — число постов в рамке, гр. — группа щита, Н — высота оси от чистого пола, мм; группы по клавишам выключателя — на листе выключателей.
4. Схема мебели, приборов и декора не является технической документацией для производства мебели; габариты — по паспортам изделий.
5. Картины и зеркала крепить к основанию по паспорту изделия (закладные и анкеры — в перечне скрытых работ); крест — ось центра предмета.
6. Двери скрытого монтажа — полотно в плоскости стены, отделка стены по полотну, плинтус прерывается у короба (узел — на листе узлов).

Допущения и предложения на листе. Основа листа: размеры сняты со скана плана заказчика по размерным цепочкам, контрольный обмер на объекте не выполнялся (К-13); высота потолка 2700 мм принята: на плане заказчика не указана (К-11); толщины стен приняты: наружные 250 мм, перегородки 150 мм (на плане 85–190 мм) (К-13); разрешённая мощность 15 кВт принята по типовой квартире, технических условий нет (К-14); утолщение стены 190 × 1360 мм и элемент 1470 × 160 мм плана заказчика не определены (К-12); ниши санузла 2 закрыты перегородкой и фальш-стеной: проектное решение, на плане заказчика ниша у входа открыта (К-18); несущие стены не определены: до технического заключения все существующие стены считаются несущими (К-20); окна существующие и сохраняются; подоконная доска и глубина откосов не заданы — приняты, не замерены (К-27); подрайон климата не задан — принят не северный (жилые от 2,5 м) (К-29). Знак «*» — принято, не замерено (замерить): К-13: отметка существующего пола; К-25: дверь пом. 8 (стена А). Знак «**» — предложено, не утверждено (согласовать). См. лист открытых вопросов (лист 7, записи К-11–К-14, К-18, К-20; лист 8, записи К-25, К-27, К-29; лист 11, запись ИЗ-20).

1000 мм · печать 1:1

Изм.	Кол.уч	Лист	№ док.	Подп.	Дата
Разраб.		Кырлан А.С.			13.11.26
Пров.					
ГИП					
Н. контр.					
Утв.					

ГД-2026-003-АИ

Трёхкомнатная квартира

Общая площадь 78,95* м² · * размеры со скана, не замерены (реестр — л. 6–11, К-13)

Дизайн-проект интерьера трёхкомнатной квартиры

Стадия	Лист	Листов
РП	113	132

Развёртки стен В, Г. Коридор (пом. 8)

М 1:25

Кырлан Александр Сергеевич


выпуск 13.11.2026 № 6f3a8abb2c · стр. 122 из 157

Узлы. Лист 1 из 2

Пороги и стыки покрытий, скрытые двери, короба стояков, гидроизоляция, плинтус

1 Порог 15 мм: мокрая зона — смежное помещение (М 1:5)


Применение: двери Д-5, Д-3; места — лист 89

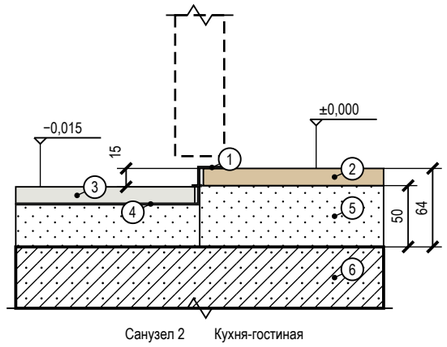

Поз.	Состав слоя, изделие
1	порог-переход металлический, перепад 15 мм, на клей-герметик
2	инженерная доска на клею
3	керамогранит на клею С2 TE S1
4	гидроизоляция в 2 слоя с подъёмом на торец ступени, лента в углу
5	ЦПС М200 50 мм; в мокрой зоне 33 мм
6	плита перекрытия

2 Стык покрытий пола Т-профилем без перепада (М 1:5)


Применение: проёмы 5↔6, 8↔5; места — лист 89

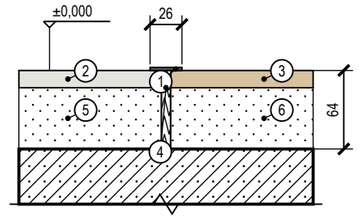

Поз.	Состав слоя, изделие
1	Т-профиль алюминиевый, полка 26 мм, ножка в шов; цвет — по покрытию
2	Прихожая: керамогранит на клею С2 TE S1
3	Кухня-гостиная: инженерная доска на клею
4	шов 8 мм по оси полотна двери, заполнитель эластичный
5	Прихожая: стяжка ЦПС М200 50 мм
6	Кухня-гостиная: стяжка ЦПС М200 50 мм

3 Дверь скрытого монтажа в плоскости стены, плинтус (М 1:5)


Применение: двери Д-2, Д-5, Д-3, Д-4; места — лист 89

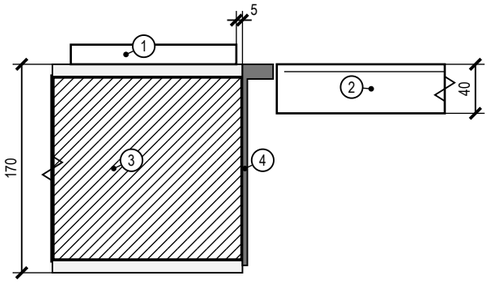

Поз.	Состав слоя, изделие
1	плинтус МДФ 80×16 на клей; у короба — зазор 5 мм, окраска в цвет стены
2	полотно 40 мм под окраску, заподлицо со стеной; теневой шов 3 мм
3	стена 150 мм, штукатурка 10 мм с двух сторон
4	короб скрытого монтажа (алюминий), лицом в плоскости отделки; монтаж до штукатурки

4 Короб стояков К1-1, В1-1 с люком и звукоизоляцией (М 1:10)

Применение: пом. 2; места — лист 89

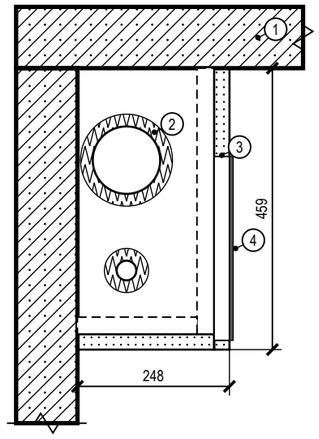

Поз.	Состав слоя, изделие
1	стены существующие — не ослаблять
2	звукоизоляция стояков рулонная 20 мм; К1-1 Ø110, В1-1 Ø32
3	короб: профиль 27×28, ГКЛВ 2×12,5 мм, облицовка плиткой
4	ревизионный люк 300×400 мм нажимной, под плитку; против ревизии стояка

Допущения и предложения на листе

Основа листа: размеры сняты со скана плана заказчика по размерным цепочкам, контрольный обмер на объекте не выполнялся (К-13); высота потолка 2700 мм принята: на плане заказчика не указана (К-11); толщины стен приняты: наружные 250 мм, перегородки 150 мм (на плане 85–190 мм) (К-13); разрешённая мощность 15 кВт принята по типовой квартире, технических условий нет (К-14); утолщение стены 190 × 1360 мм и элемент 1470 × 160 мм плана заказчика не определены (К-12); ниши санузла 2 закрыты перегородкой и фальш-стеной: проектное решение, на плане заказчика ниша у входа открыта (К-18); несущие стены не определены: до технического заключения все существующие стены считаются несущими (К-20); окна существующие и сохраняются; подоконная доска и глубина откосов не заданы — приняты, не замерены (К-27); подрайон климата не задан — принят не северный (жилые от 2,5 м) (К-29).

Открытые вопросы и конфликты по листу: К-25.

См. лист открытых вопросов (лист 7, записи К-11–К-14, К-18, К-20; лист 8, записи К-25, К-27, К-29).

Условные обозначения

- железобетон (плита, стены) — условно: конструкция не установлена
- кладка, перегородка — условно: конструкция не установлена
- стяжка, раствор
- гипсокартон ГКЛВ
- звукоизоляция, эластичный заполнитель
- плитка, керамогранит на клею
- инженерная доска (покрытие пола)
- металлический профиль (порог, Т-профиль, короб двери)
- гидроизоляция (обмазочная, лента)

Примечания

1. Узлы — типовые решения проекта для мест, отмеченных выносками на листе схемы расположения развёрток и узлов; размеры — в мм, отметки — в м от ±0,000.
2. Узлы с гидроизоляцией, закладными и коробами скрытого монтажа принимаются по актам скрытых работ до закрытия отделкой; гидроизоляция — после теста проливом (24 ч).
3. Марки изделий (порог, Т-профиль, короб скрытой двери, люк) — по спецификациям; замена — на аналог с теми же габаритами по согласованию с автором проекта.
4. Материал плиты перекрытия и стен в узлах показан условно (железобетон, кладка): конструкция дома не установлена — крепёж, анкеры и толщины слоёв уточняются после обследования (до него — по допущениям общих указаний).
5. Узлы комплекта выпущены на 2 листах, нумерация узлов сквозная: 1–4 — лист 114 альбома (данный лист); 5–7 — лист 115 альбома.

Изм.	Кол.уч	Лист	№ док.	Подп.	Дата
Разраб.		Кырлан А.С.			13.11.26
Пров.					
ГИП					
Н. контр.					
Утв.					

ГД-2026-003-АИ

Трёхкомнатная квартира

Общая площадь 78,95* м² · * размеры со скана, не замерены (реестр — л. 6–11, К-13)

Дизайн-проект интерьера трёхкомнатной квартиры

Стадия	Лист	Листов
РП	114	132

Узлы. Лист 1 из 2

М 1:5; 1:10

Кырлан Александр Сергеевич


выпуск 13.11.2026 № 6f3a8abb2c · стр. 123 из 157

Узлы. Лист 2 из 2

Пороги и стыки покрытий, скрытые двери, короба стояков, гидроизоляция, плинтус

5 Гидроизоляция санузла: заход на стены 200 мм, примыкание ванны (М 1:10)


Применение: пом. 2, 7; места — лист 89

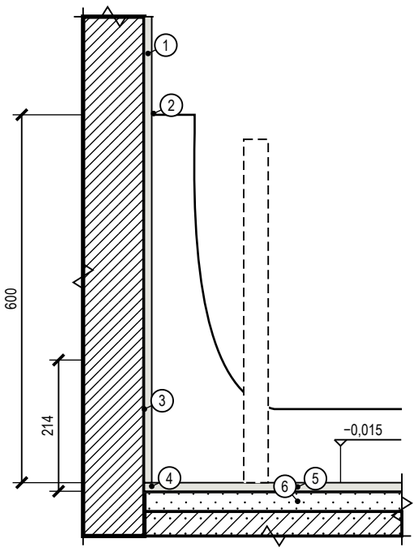

Поз.	Состав слоя, изделие
1	облицовка — плитка на клею C2 TE S1, затирка CG2WA
2	примыкание ванны: лента бордюрная + силиконовый санитарный герметик; облицовка опирается на борт
3	гидроизоляция обмазочная в 2 слоя, заход на стены 200 мм (в зоне душа выше), до облицовки; акт скрытых работ, тест проливом
4	лента гидроизоляционная в углах и у трапов
5	керамогранит на клею C2 TE S1
6	ЦПС М200 33 мм

6 Плинтус МДФ 80×16 мм у окрашенной стены по доске (ламинату) (М 1:5)


Применение: пом. 1, 3, 4, 6, 8; места — лист 89

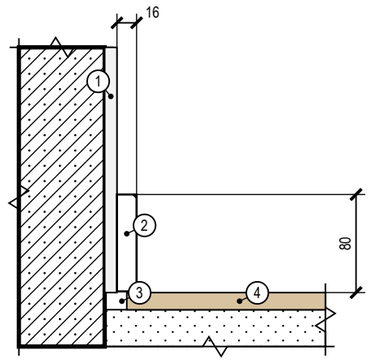

Поз.	Состав слоя, изделие
1	штукатурка, шпаклёвка Q3, окраска — по ведомости отделки
2	плинтус МДФ 80×16 под окраску в цвет стены; клей монтажный — к стене, не к полу
3	зазор покрытия у стены 8–10 мм закрывается плинтусом
4	инженерная доска на клею

7 Плинтус МДФ 80×16 мм у окрашенной стены по керамограниту (плитке) (М 1:5)

Применение: пом. 5; места — лист 89

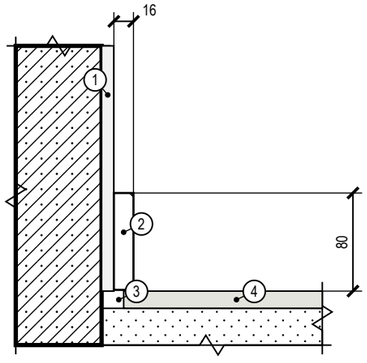

Поз.	Состав слоя, изделие
1	штукатурка, шпаклёвка Q3, окраска — по ведомости отделки
2	плинтус МДФ 80×16 под окраску в цвет стены; клей монтажный — к стене, не к полу
3	зазор покрытия у стены 8–10 мм закрывается плинтусом
4	керамогранит на клею C2 TE S1

Допущения и предложения на листе

Основа листа: размеры сняты со скана плана заказчика по размерным цепочкам, контрольный обмер на объекте не выполнялся (К-13); высота потолка 2700 мм принята: на плане заказчика не указана (К-11); толщины стен приняты: наружные 250 мм, перегородки 150 мм (на плане 85–190 мм) (К-13); разрешённая мощность 15 кВт принята по типовой квартире, технических условий нет (К-14); утолщение стены 190 × 1360 мм и элемент 1470 × 160 мм плана заказчика не определены (К-12); ниши санузла 2 закрыты перегородкой и фальш-стеной: проектное решение, на плане заказчика ниша у входа открыта (К-18); несущие стены не определены: до технического заключения все существующие стены считаются несущими (К-20); окна существующие и сохраняются; подоконная доска и глубина откосов не заданы — приняты, не замерены (К-27); подрайон климата не задан — принят не северный (жилые от 2,5 м) (К-29).

См. лист открытых вопросов (лист 7, записи К-11–К-14, К-18, К-20; лист 8, записи К-27, К-29).

Условные обозначения

- железобетон (плита, стены) — условно: конструкция не установлена
- кладка, перегородка — условно: конструкция не установлена
- стяжка, раствор
- плитка, керамогранит на клею
- инженерная доска (покрытие пола)
- гидроизоляция (обмазочная, лента)

Примечания

1. Узлы — типовые решения проекта для мест, отмеченных выносками на листе схемы расположения развёрток и узлов; размеры — в мм, отметки — в м от ±0,000.
2. Узлы с гидроизоляцией, закладными и коробами скрытого монтажа принимаются по актам скрытых работ до закрытия отделкой; гидроизоляция — после теста проливом (24 ч).
3. Марки изделий (порог, Т-профиль, короб скрытой двери, люк) — по спецификациям; замена — на аналог с теми же габаритами по согласованию с автором проекта.
4. Материал плиты перекрытия и стен в узлах показан условно (железобетон, кладка): конструкция дома не установлена — крепёж, анкеры и толщины слоёв уточняются после обследования (до него — по допущениям общих указаний).
5. Узлы комплекта выпущены на 2 листах, нумерация узлов сквозная: 1–4 — лист 114 альбома; 5–7 — лист 115 альбома (данный лист).

Изм.	Кол.уч	Лист	№ док.	Подп.	Дата			
Разраб.		Кырлан А.С.			13.11.26	ГД-2026-003-АИ		
Пров.						Трёхкомнатная квартира Общая площадь 78,95* м² · * размеры со скана, не замерены (реестр — л. 6–11, К-13)		
ГИП						Дизайн-проект интерьера трёхкомнатной квартиры	Стадия: РП	Лист: 115 / Листов: 132
Н. контр.						Узлы. Лист 2 из 2 М 1:10; 1:5	Кырлан Александр Сергеевич	
Утв.								

выпуск 13.11.2026 № 6f3a8abb2c · стр. 124 из 157

10

Смета

Кырлан Александр Сергеевич

выпуск 13.11.2026 · 6f3a8abb2c · стр. 125 из 157

Ведомость объёмов работ

Объёмы по помещениям от чертежа · площади в м², длины в м · формула, правило проёмов и источник в каждой строке

Ведомость объёмов работ по помещениям

Поз.	Наименование работ (материал, число слоёв)	Ед. изм.	Объём по помещениям (№ по экспликации)								Всего	Формула подсчёта	Правило проёмов	Источник	Цена за ед., ₽	Стоимость, ₽
			1	2	3	4	5	6	7	8						
1. Демонтаж и черновые работы																
1	Демонтаж существующего покрытия пола до основания	м²	17,75	4,43	1,85	12,80	7,13	29,20	2,29	3,50	78,95	S пом.		л. 27–29	по КП	
2	Демонтаж существующей отделки стен до основания	м²	39,17	18,61	14,74	32,44	21,86	51,56	13,10	14,17	205,65	P × H − проёмы	за вычетом проёмов	л. 27–29	по КП	
3	Демонтаж существующей отделки потолка до основания	м²	17,75	4,43	1,85	12,80	7,13	29,20	2,29	3,50	78,95	S пом.		л. 27–29	по КП	
4	Демонтаж существующих дверных блоков	шт	1			1	1	1		2	6	по ведомости проёмов		л. 28–30	по КП	
5	Демонтаж существующих сантехприборов и электрооборудования (если есть)	компл										по факту на объекте		л. 28, 29	по КП	
6	Монтаж каркасной перегородки П-1** (С112): каркас ПС усиленный через 400 мм, ГКЛВ в 2 слоя с каждой стороны, обрамление проёма профилем УА; предложение, пока П-1** не утверждена автором (К-18, К-4)	м²									2,85	1,60 × 2,70 − 1,47 (Д-5 700 × 2100) = 2,85 м², одна сторона; пом. 6, 7	проёмы вычтены	л. 28, 29, 58	2 700	7 695
7	Облицовка (фальш-стена) П-2**: ГКЛВ в 2 слоя по раме инсталляции под плитку; предложение, пока П-2** не утверждена автором (К-18)	м²									1,58	0,66 × 2,39 = 1,58 м², одна сторона; пом. 7	проёмы вычтены	л. 28, 29, 58	1 050	1 659
8	Заполнение каркаса П-1** минераловатной плитой (звукоизоляция, Rw 51 дБ); предложение, пока П-1** не утверждена автором (К-18, К-4)	м²									2,85	2,85 м² без проёма		л. 58	по КП	
9	Шпаклёвка швов ГКЛВ П-1** под плитку (Q1), сторона санузла; предложение, пока П-1** не утверждена автором (К-18, К-4)	м²									2,85	2,85 м² стороны, облицованной плиткой; сторона под окраску — в строке шпаклёвки стен помещения		л. 58, 67, 68	по КП	
10	Шпаклёвка швов ГКЛВ П-2** под плитку (Q1), сторона санузла; предложение, пока П-2** не утверждена автором (К-18)	м²									1,58	1,58 м² стороны, облицованной плиткой; сторона под окраску — в строке шпаклёвки стен помещения		л. 58, 67, 68	по КП	
11	Устройство стяжки: стяжка ЦПС М200, 50 мм	м²	17,81	4,49	1,91	12,86	7,45	29,37	2,34	3,83	80,06	S пом. + S в дверных проёмах (b × t/2)	проёмы добавлены	л. 66–68	530	42 432
12	Гидроизоляция обмазочная, 2 слоя: пол, стены на 200 мм, зоны замачивания	м²		10,95					7,20		18,15	пол + (P − двери) × h заведения + зоны замачивания		л. 62	450	8 167
13	Штукатурка стен по маякам, до 10 мм	м²	39,17	18,61	14,74	32,44	21,86	48,71	8,67	14,17	198,37	P × H − проёмы по обводу коробок − грани перегородок на ГКЛВ	за вычетом проёмов	л. 27, 67, 68	530	105 136
14	Штукатурка оконных откосов шириной до 200 мм	м²	0,92			0,78		1,58			3,28	Σ (2h + b) × глубина откоса	откосы ≤ 200 мм	л. 27	540	1 771
15	Потолок ГКЛ по каркасу П113, 1 слой	м²	17,75	4,43		12,80	7,13	29,20	2,29	3,50	77,10	S пом. по плану потолков		л. 59–61	1 500	115 650
Итого по разделу 1 — 282 510 ₽ (позиций 15, из них по КП 8); в сводную смету — л. 123, 124																
2. Инженерные системы																
16	Прокладка кабеля ВВГнг(А)-LS по группам щита: за потолком и в штробах стен (штробы — только после технического заключения, см. строку «Штробы в стенах»)	м									493,50	Σ длин групп щита		л. 42	60	29 610
17	Прокладка слаботочной линии: Кабель домофона — тип по системе поставщика, отдельно от силовых	м									2,90	по лучам от ЩС**: 1 точ., запас 10 %		л. 45	по КП	

Допущения и предложения на листе

Основа листа: размеры сняты со скана плана заказчика по размерным цепочкам, контрольный обмер на объекте не выполнялся (К-13); высота потолка 2700 мм принята: на плане заказчика не указана (К-11); толщины стен приняты: наружные 250 мм, перегородки 150 мм (на плане 85–190 мм) (К-13); разрешённая мощность 15 кВт принята по типовой квартире, технических условий нет (К-14); утолщение стены 190 × 1360 мм и элемент 1470 × 160 мм плана заказчика не определены (К-12); ниши санузла 2 закрыты перегородкой и фальш-стеной: проектное решение, на плане заказчика ниша у входа открыта (К-18); несущие стены не определены: до технического заключения все существующие стены считаются несущими (К-20); окна существующие и сохраняются; подоконная доска и глубина откосов не заданы — приняты, не замерены (К-27); подрайон климата не задан — принят не северный (жилые от 2,5 м) (К-29).

Знак «**» — предложение проектировщика, заказчиком не утверждено (согласовать с заказчиком): ИЗ-9, ИЗ-17, К-7: ЩС — щит слаботочный: место и состав; К-4, К-18: П-1 — проектное решение исполнителя: на плане заказчика ниша у входа открыта в кухню-гостиную; конструкция не утверждена автором (вопрос К-18), положение и размеры сняты со скана (К-13); К-18: П-2 — проектное решение исполнителя: на плане заказчика у наружной стены уступ 660 × 260 мм; конструкция не утверждена автором (вопрос К-18).

Открытые вопросы и конфликты по листу: К-28.

См. лист открытых вопросов (лист 6, записи К-4, К-7; лист 7, записи К-11–К-14, К-18, К-20; лист 8, записи К-27–К-29; лист 9, запись ИЗ-9; лист 11, запись ИЗ-17).

Изм.	Кол.уч	Лист	№ док.	Подп.	Дата
Разраб.		Кырлан А.С.			13.11.26
Пров.					
ГИП					
Н. контр.					
Утв.					

ГД-2026-003-АИ

Трёхкомнатная квартира

Общая площадь 78,95* м² · * размеры со скана, не замерены (реестр — л. 6–11, К-13)

Дизайн-проект интерьера трёхкомнатной квартиры

Стадия	Лист	Листов
РП	116	132

Ведомость объёмов работ

М б/м

Кырлан Александр Сергеевич

Ведомость объёмов работ (продолжение)

Объёмы по помещениям от чертежа · площади в м², длины в м · формула, правило проёмов и источник в каждой строке

Ведомость объёмов работ по помещениям (продолжение)

Поз.	Наименование работ (материал, число слоёв)	Ед. изм.	Объём по помещениям (№ по экспликации)								Всего	Формула подсчёта	Правило проёмов	Источник	Цена за ед., ₽	Стоимость, ₽
			1	2	3	4	5	6	7	8						
18	Прокладка слаботочной линии: Кабель коаксиальный RG-6 (75 Ом) к розеткам ТВ, отдельно от силовых	м									30,30	по лучам от ЩС**: 2 точ., запас 10 %		л. 45	по КП	
19	Прокладка слаботочной линии: Кабель U/UTP кат. 6 (LAN, Wi-Fi и камеры по PoE), отдельно от силовых	м									62,30	по лучам от ЩС**: 5 точ., запас 10 %		л. 45	по КП	
20	Прокладка гофротрубы Ø20 для слаботочных линий, отдельно от силовых	м									86,00	по длине лучей без участков в канале плинтуса (≈ 90 %)		л. 45	140	12 040
21	Сборка слаботочного щита ЩС**: корпус, патч-панель, подключение линий и питания 220 В; коммутатор и точки доступа — оборудование заказчика	шт									1	один щит		л. 40, 41, 45	по КП	
22	Электроточка: подрозетник в бетоне, розетка, выключатель, вывод	шт	10	4		11	8	27	3	4	67	по ведомости электроточек		л. 37, 40, 41	950	63 650
23	Штробы в стенах под спуски кабеля к точкам — выполняются только после технического заключения о несущих стенах	м	18,00	4,51		19,60	11,84	41,35	3,17	7,48	105,95	Σ (H − h) по точкам на стенах: вертикальные спуски	после техзаключения	л. 28, 29, 37	по КП	
24	Установка встраиваемого точечного светильника	шт	8	3		6	4	14	2	2	39	по плану освещения		л. 38	750	29 250
25	Монтаж светильника: потолочного, подвесного, настенного	шт	2	1	1	2		3	1		10	по плану освещения		л. 38	1 200	12 000
26	Монтаж LED-ленты в алюминиевый профиль	м	15,50			12,30	1,80	25,10			54,70	Σ длин лент по плану освещения		л. 38	230	12 581
27	Установка блока питания LED в доступном месте (люк, шкаф)	шт	1			1	1	2			5	один на LED-группу		л. 38	570	2 850
28	Установка автономного пожарного извещателя	шт	1			1	1	2		1	6	по плану розеток		л. 37	по КП	
29	Сборка щита: установка автоматов и АВДТ групп, вводного автомата	шт									15	группы + вводной автомат		л. 42	230	3 450
30	Установка вводного УЗО	шт									1	по однолинейной схеме		л. 42	380	380
31	Монтаж инсталляции, установка подвесного унитаза и кнопки смыва	шт		1					1		2	по плану выводов		л. 48, 56	10 500	21 000
32	Короб инсталляции: каркас и обшивка ГКЛВ в 2 слоя, ревизионный доступ к смыву	шт		1					1		2	по плану выводов		л. 48, 62–65	по КП	
33	Короб стояков Ш1 248 × 459 мм (внутренний 195 × 406): каркас и обшивка ГКЛВ в 2 слоя, ревизионный люк 300 × 400	м²		1,70							1,70	свободный периметр короба × H помещения		л. 27, 48	по КП	
34	Короб К1 над чистым полом: каркас и обшивка ГКЛВ под плитку (материалы — в спецификации ВК)	м.п.		0,85					1,32		2,17	Σ открытых участков выпусков К1 (профиль листа разводки ВК)		л. 48, 56	по КП	
35	Установка ванны с сифоном	шт		1							1	по плану выводов		л. 48, 56	6 000	6 000
36	Установка умывальника (мойки) с сифоном и смесителем	шт		1				1	1		3	по плану выводов		л. 48, 56	3 000	9 000
37	Установка душевого поддона с трапом, ограждения	шт							1		1	по плану выводов		л. 48, 56	по КП	
38	Подключение стиральной (посудомоечной) машины к ВК	шт		1				1			2	по плану выводов		л. 48	по КП	
39	Установка радиатора с узлом подключения и терморегулятором	шт	1			1		2			4	по плану отопления		л. 47	по КП	

Допущения и предложения на листе

Основа листа: размеры сняты со скана плана заказчика по размерным цепочкам, контрольный обмер на объекте не выполнялся (К-13); высота потолка 2700 мм принята: на плане заказчика не указана (К-11); толщины стен приняты: наружные 250 мм, перегородки 150 мм (на плане 85–190 мм) (К-13); разрешённая мощность 15 кВт принята по типовой квартире, технических условий нет (К-14); утолщение стены 190 × 1360 мм и элемент 1470 × 160 мм плана заказчика не определены (К-12); ниши санузла 2 закрыты перегородкой и фальш-стеной: проектное решение, на плане заказчика ниша у входа открыта (К-18); несущие стены не определены: до технического заключения все существующие стены считаются несущими (К-20); окна существующие и сохраняются; подоконная доска и глубина откосов не заданы — приняты, не замерены (К-27); подрайон климата не задан — принят не северный (жилые от 2,5 м) (К-29).

Знак «**» — предложение проектировщика, заказчиком не утверждено (согласовать с заказчиком): ИЗ-9, ИЗ-17, К-7: ЩС — щит слаботочный: место и состав.

Открытые вопросы и конфликты по листу: К-28.

См. лист открытых вопросов (лист 6, запись К-7; лист 7, записи К-11–К-14, К-18, К-20; лист 8, записи К-27–К-29; лист 9, запись ИЗ-9; лист 11, запись ИЗ-17).

Изм.	Кол.уч	Лист	№ док.	Подп.	Дата
Разраб.		Кырлан А.С.			13.11.26
Пров.					
ГИП					
Н. контр.					
Утв.					

ГД-2026-003-АИ

Трёхкомнатная квартира

Общая площадь 78,95* м² · * размеры со скана, не замерены (реестр — л. 6–11, К-13)

Дизайн-проект интерьера трёхкомнатной квартиры

Стадия	Лист	Листов
РП	117	132

Ведомость объёмов работ (продолжение)

М б/м

Кырлан Александр Сергеевич

Ведомость объёмов работ (продолжение)

Объёмы по помещениям от чертежа · площади в м², длины в м · формула, правило проёмов и источник в каждой строке

Ведомость объёмов работ по помещениям (продолжение)

Поз.	Наименование работ (материал, число слоёв)	Ед. изм.	Объём по помещениям (№ по экспликации)								Всего	Формула подсчёта	Правило проёмов	Источник	Цена за ед., ₽	Стоимость, ₽
			1	2	3	4	5	6	7	8						
Итого по разделу 2 — 201 811 ₽ (позиций 24, из них по КП 12); в сводную смету — л. 123, 124																
3. Чистовые работы																
40	Облицовка стен керамогранитом 600×1200 на клею	м²		16,00					12,38		28,38	по раскладке: зона облицовки − место за коробом	за вычетом проёмов	л. 62–65	2 500	70 950
41	Облицовка короба инсталляции (ГКЛВ) керамогранитом: лицо, боковины, полка	м²		3,41					1,47		4,88	по раскладке: лицо, боковины, полка		л. 62–65	2 500	12 200
42	Облицовка фартука керамогранитом 1200×600	м²						1,85			1,85	по раскладке фартука		л. 62–65, 67, 68	2 400	4 440
43	Укладка керамогранита на пол, 600×600, на клею	м²		4,49			7,45		2,34		14,28	S пом. + S в дверных проёмах	проёмы добавлены	л. 62–66	1 800	25 704
44	Затирка швов керамогранита	м²		23,84			7,13	1,85	16,14		48,96	Σ S облицовки и пола из плитки		л. 62–65	150	7 344
45	Грунтование стен, 2 слоя (под штукатурку и под отделку)	м²	39,17	18,61	14,74	32,44	21,86	51,56	13,10	14,17	205,65	P × H − проёмы	за вычетом проёмов	л. 67, 68	96	19 742
46	Шпаклёвка стен под окраску, 2 слоя (старт и финиш), уровень Q3	м²	39,17		14,74	32,44	21,86	49,71		14,17	172,09	P × H − проёмы − фартук	за вычетом проёмов	л. 67, 68	750	129 068
47	Грунтование и шпаклёвка оконных откосов, 2 слоя	м.п.	5,10			4,32		8,77			18,19	Σ (2h + b) по окнам	по окнам	л. 27	300	5 457
48	Грунтование потолка, 2 слоя	м²	17,75	4,43	1,85	12,80	7,13	29,20	2,29	3,50	78,95	S пом.		л. 67, 68	96	7 579
49	Шпаклёвка потолка под окраску, 2 слоя, уровень Q3	м²	17,75	4,43	1,85	12,80	7,13	29,20	2,29	3,50	78,95	S пом.		л. 59–61, 67, 68	950	75 003
50	Окраска потолка водно-дисперсионной краской, 2 слоя	м²	17,75	4,43	1,85	12,80	7,13	29,20	2,29	3,50	78,95	S пом.		л. 67, 68	360	28 422
51	Окраска стен водно-дисперсионной краской, 2 слоя	м²	44,00		16,42	36,10	30,13	59,30		23,48	209,43	P × H − фартук, проёмы не вычитаются	без вычета проёмов	л. 67, 68	300	62 829
52	Окраска оконных откосов, 2 слоя	м.п.	5,10			4,32		8,77			18,19	Σ (2h + b) по окнам	по окнам	л. 27	120	2 183
53	Укладка инженерной доски на клей	м²	17,81		1,91	12,86		29,37		3,83	65,78	S пом. + S в дверных проёмах	проёмы добавлены	л. 66–68	1 200	78 936
54	Установка плинтуса МДФ h=80 мм	м.п.	16,80		5,28	13,64	7,85	22,24		4,53	70,34	P − ширина дверных проёмов		л. 67, 68	450	31 653
55	Окраска плинтуса в тоне No. 241, 2 слоя	м.п.	16,80		5,28	13,64	7,85	22,24		4,53	70,34	как плинтус		л. 67, 68	300	21 102
56	Монтаж дверей скрытого монтажа под покраску (поставщик дверей)	шт	1			1		1		2	5	по ведомости проёмов		л. 30	5 250	26 250
57	Входная дверь, поставка с монтажом и откосами	шт									1	по ведомости проёмов		л. 30	по КП	
58	Монтаж телевизора C12** на кронштейн, скрытая прокладка HDMI и питания (штроба, трубка), подключение акустики	шт				1		1			2	по плану расстановки		л. 86	по КП	
Итого по разделу 3 — 608 862 ₽ (позиций 19, из них по КП 2); в сводную смету — л. 123, 124																

Допущения и предложения на листе

Основа листа: размеры сняты со скана плана заказчика по размерным цепочкам, контрольный обмер на объекте не выполнялся (К-13); высота потолка 2700 мм принята: на плане заказчика не указана (К-11); толщины стен приняты: наружные 250 мм, перегородки 150 мм (на плане 85–190 мм) (К-13); разрешённая мощность 15 кВт принята по типовой квартире, технических условий нет (К-14); утолщение стены 190 × 1360 мм и элемент 1470 × 160 мм плана заказчика не определены (К-12); ниши санузла 2 закрыты перегородкой и фальш-стеной: проектное решение, на плане заказчика ниша у входа открыта (К-18); несущие стены не определены: до технического заключения все существующие стены считаются несущими (К-20); окна существующие и сохраняются; подоконная доска и глубина откосов не заданы — приняты, не замерены (К-27); подрайон климата не задан — принят не северный (жилые от 2,5 м) (К-29).

Знак «**» — предложение проектировщика, заказчиком не утверждено (согласовать с заказчиком): К-7: C12 — На плане и в спецификации мебели телевизора в пом. 4 не было, при этом точки TB2, LAN2 и P12 «ТВ над комодом» заданы.

Открытые вопросы и конфликты по листу: К-28.

См. лист открытых вопросов (лист 6, запись К-7; лист 7, записи К-11–К-14, К-18, К-20; лист 8, записи К-27–К-29).

Изм.	Кол.уч	Лист	№ док.	Подп.	Дата
Разраб.		Кырлан А.С.			13.11.26
Пров.					
ГИП					
Н. контр.					
Утв.					

ГД-2026-003-АИ

Трёхкомнатная квартира

Общая площадь 78,95* м² · * размеры со скана, не замерены (реестр — л. 6–11, К-13)

Дизайн-проект интерьера трёхкомнатной квартиры

Стадия	Лист	Листов
РП	118	132

Ведомость объёмов работ (продолжение)

М б/м

Кырлан Александр Сергеевич

Ведомость объёмов работ (окончание)

Объёмы по помещениям от чертежа · площади в м², длины в м · формула, правило проёмов и источник в каждой строке

Ведомость подсчёта площадей по помещениям

№	Помещение	S пола, м²	P, м	H, м	P × H, м²	Проёмы, м²	Стены нетто, м²	В дверных проёмах, м²	Плинтус, м	Откосы, м.п.
1	Спальня 1	17,75	17,60	2,50	44,00	4,83	39,17	0,06	16,80	5,10
2	Ванная	4,43	8,44	2,40	20,29	1,68	18,61	0,06	нет	нет
3	Гардеробная	1,85	6,08	2,70	16,42	1,68	14,74	0,06	5,28	нет
4	Спальня 2	12,80	14,44	2,50	36,10	3,66	32,44	0,06	13,64	4,32
5	Прихожая	7,13	11,50	2,62	30,13	8,27	21,86	0,32	7,85	нет
6	Кухня-гостиная	29,20	24,46	2,50	61,15	9,59	51,56	0,17	22,24	8,77
7	Санузел 2	2,29	6,06	2,40	14,57	1,47	13,10	0,05	нет	нет
8	Коридор	3,50	8,96	2,62	23,48	9,30	14,17	0,33	4,53	нет
	Итого	**78,95**			**246,13**	**40,49**	**205,64**	**1,11**	**70,34**	**18,19**

Реестр контрольных сумм

Показатель	По ВОР	По чертежу	Расхождение	Лист
Σ площадей помещений без летних, м² — общая площадь по экспликации	78,95	78,95	0,0 %	л. 27
Стены под окраску, м² (шпаклёвка) ведомость отделки	172,09	172,08	0,0 %	л. 67, 68
Потолки под окраску, м² — ведомость отделки	78,95	78,95	0,0 %	л. 67, 68
Плинтус, м — ведомость отделки	70,34	70,34	0,0 %	л. 67, 68
Плитка к заказу, шт — ведомость плитки	125	125	0,0 %	л. 62
Гидроизоляция, м² — ведомость материалов плитки	18,15	18,15	0,0 %	л. 62
Точки ЭОМ, шт — планы ЭОМ (без щитов)	132	134	-1,5 %	л. 37, 38

Примечания

1. Объёмы — от геометрии проекта (та же, что на планах и в ведомости отделки), не от общей площади: P — периметр чистого контура, H — от чистого пола до низа потолка, проёмы — по наружному обводу коробок.
2. Подсчёт по ГЭСН-2001-15 и ГЭСН-2001-11: штукатурка и шпаклёвка стен — за вычетом проёмов; окраска водными составами — без вычета проёмов (п. 2.24); откосы — отдельно, по ширине до 200 и более 200 мм; полы — с площадью в дверных проёмах.
3. Плитка — по раскладке (целые и с подрезкой); короб инсталляции и фартук — отдельными строками, двойного счёта облицовки нет. Материалы, запас и количество к заказу — в спецификации материалов.
4. Цены — ориентир по открытым прайсам Москвы (прайсы собраны 21.09.2026, часть расценок сверена повторно 06.10.2026 и 08.11.2026), не коммерческое предложение; «по КП» — расценки нет, строка в итог не входит.
5. Демонтаж — по плану демонтажа и общим указаниям: покрытия пола, отделка стен и потолков, дверные блоки — до основания; объёмы справочные — по плану демонтажа (расценки в книге нет — «по КП»).
6. Штробы в стенах — только после технического заключения о несущих стенах (общие указания, план обмера и демонтажа): строка «Штробы в стенах» вертикальные спуски кабеля от потолочной трассы к точкам, объём не меньше фактического (горизонтальные трассы — по исполнительной схеме). Расценки штробления в прайсе нет — «по КП», в итог не входит; кабель в штробах стен прокладывается после неё.
7. Площадь облицовки стен — одно число с тремя названиями: зона облицовки по ведомости отделки 31,71 м² − место за коробом инсталляции 3,33 м² (плитку туда не кладут) = стены под плитку 28,38 м² (строка «Облицовка стен»); облицовка коробов 4,88 м² — отдельной строкой; стены и короба вместе — 33,26 м² (столько плитки по раскладке в спецификации). Источник — один (quantities.js), расхождение на листах ловит.
8. Слаботочные сети: кабель по лучам от ЩС** 95,50 м (U/UTP, RG-6, домофон — по видам), гофра 86,00 м, щит ЩС** с патч-панелью; розетки RJ45 и ТВ монтируются в строке «Электроточка». Длины те же, что в ведомости изделий электрика (одна модель — lowcurrent-engineer/bom.js); оборудование заказчика (точки доступа, камеры, коммутатор) в спецификацию не входит. 2 точ. — предложение листа слаботочки.
9. Перегородки и облицовки ГКЛ (П-1** — 2,85 м², П-2** — 1,58 м²): площадь одной стороны за вычетом проёмов, из той же модели, по которой выпущена схема каркаса; обшивка, профиль и заполнение — в спецификации материалов. П-1**, П-2** — предложение проектировщика, автором не утверждено: деньги заложены на решение, которое может измениться. Грани перегородок на ГКЛВ вычтены из штукатурки стен (7,28 м²): штукатурят основание, а не обшивку.
10. Коробы: стояков (Ш1 — 1,70 м²) и К1 над чистым полом (2,17 м открытых участков; труба К1 вдоль стен 15,72 м в короб не зашивается — она за приборами, в раме инсталляции и в шахтах). В спецификации ВК короб К1 заказывается с запасом 10 % — 2,40 м. Материалы коробов стояков и инсталляции — в спецификации материалов, К1 — в спецификации ВК.

Допущения и предложения на листе

Основа листа: размеры сняты со скана плана заказчика по размерным цепочкам, контрольный обмер на объекте не выполнялся (К-13); высота потолка 2700 мм принята: на плане заказчика не указана (К-11); толщины стен приняты: наружные 250 мм, перегородки 150 мм (на плане 85–190 мм) (К-13); разрешённая мощность 15 кВт принята по типовой квартире, технических условий нет (К-14); утолщение стены 190 × 1360 мм и элемент 1470 × 160 мм плана заказчика не определены (К-12); ниши санузла 2 закрыты перегородкой и фальш-стеной: проектное решение, на плане заказчика ниша у входа открыта (К-18); несущие стены не определены: до технического заключения все существующие стены считаются несущими (К-20); окна существующие и сохраняются; подоконная доска и глубина откосов не заданы — приняты, не замерены (К-27); подрайон климата не задан — принят не северный (жилые от 2,5 м) (К-29).

Знак «**» — предложение проектировщика, заказчиком не утверждено (согласовать с заказчиком): ИЗ-9, ИЗ-17, К-7: ЩС — щит слаботочный: место и состав; К-4, К-18: П-1 — проектное решение исполнителя: на плане заказчика ниша у входа открыта в кухню-гостиную; конструкция не утверждена автором (вопрос К-18), положение и размеры сняты со скана (К-13); К-18: П-2 — проектное решение исполнителя: на плане заказчика у наружной стены уступ 660 × 260 мм; конструкция не утверждена автором (вопрос К-18).

Открытые вопросы и конфликты по листу: К-28.

См. лист открытых вопросов (лист 6, записи К-4, К-7; лист 7, записи К-11–К-14, К-18, К-20; лист 8, записи К-27–К-29; лист 9, запись ИЗ-9; лист 11, запись ИЗ-17).

						ГД-2026-003-АИ	
						Трёхкомнатная квартира	
						Общая площадь 78,95* м² · * размеры со скана, не замерены (реестр — л. 6–11, К-13)	
Изм.	Кол.уч	Лист	№ док.	Подп.	Дата	Дизайн-проект интерьера трёхкомнатной квартиры	Стадия: РП · Лист: 119 · Листов: 132
Разраб.		Кырлан А.С.			13.11.26		
Пров.							
ГИП							
Н. контр.						**Ведомость объёмов работ (окончание)** М б/м	**Кырлан Александр Сергеевич**
Утв.							

Спецификация материалов

Отделочные материалы: чистое количество, запас, упаковка, к заказу · ГОСТ 21.110-2013

Спецификация материалов (ГОСТ 21.110-2013, форма 1)

Поз.	Наименование и техническая характеристика	Тип, марка, артикул	Код продукции	Поставщик	Ед. изм.	Количество				Масса ед., кг	Примечание
						чистое	запас, %	упаковка	к заказу		
Покрытия полов и облицовка											
1	Инженерная доска (дуб натуральный, рабочий слой 4 мм, эмиссия E1, прямая укладка)	аналог: инженерная доска, дуб натуральный, масло, 1-полосная, 14/4 мм			м²	65,78	7	по артикулу	70,40 м²		пом. 1, 3, 4, 6, 8; до целой упаковки; л. 66–68
2	Клей для паркетной и инженерной доски (эластичный, по ТУ изготовителя доски)	по выбору подрядчика			м²	65,78		ведро по ТУ	по ТУ		расход кг/м² — по ТУ клея; л. 66
3	Керамогранит 600×600 мм под травертин	аналог: керамогранит под травертин			шт	24	10	коробка	27 шт		4 целых + 20 с подрезкой; 6,72 м² по раскладке, к заказу 9,72 м²; пом. 2, 7; л. 62–65
4	Керамогранит 600×1200 мм под травертин	аналог: керамогранит под травертин			шт	67	10	коробка	79 шт		15 целых + 52 с подрезкой; 33,26 м² по раскладке, к заказу 56,88 м²; пом. 2, 7; л. 62–65
5	Керамогранит 600×1200 мм ректифицированный под травертин, матовый	аналог: керамогранит ректифицированный под травертин, матовый			шт	12	10	коробка	14 шт		2 целых + 10 с подрезкой; 7,13 м² по раскладке, к заказу 10,08 м²; пом. 5; л. 62–65
6	Керамогранит 1200×600 мм под травертин, матовый	аналог: керамогранит под травертин, матовый			шт	4	10	коробка	5 шт		0 целых + 4 с подрезкой; 1,85 м² по раскладке, к заказу 3,60 м²; пом. 6; л. 62–65
Сухие смеси и гидроизоляция											
7	Клей плиточный цементный класса C2 TE S1 (ГОСТ Р 56387-2018)	Ceresit CM 17 или аналог			кг	278,81	10	мешок 25 кг	13 меш.	25	слой 5 мм, 1,20 кг/м² на 1 мм; л. 62
8	Затирка цементная класса CG2WA, цвет — по колерной карте	Mapei Ultracolor Plus 132 или аналог			кг	3,47	10	упак. 2 кг	2 упак.	2	расход (a+b)/ab × шов × t × 1,6 кг/м²; л. 62
9	Гидроизоляция обмазочная полимерная, 2 слоя, лента в углах, манжеты на выводах	по выбору подрядчика			м²	18,15	10	ведро по ТУ	по ТУ		пом. 2, 7; расход кг/м² — по ТУ; л. 62
10	Лента демпферная по периметру пола из плитки	по выбору подрядчика			м	20,36	10	рулон	23,00 м		л. 62
11	Смесь цементно-песчаная для стяжки М200 (50 мм, 33 мм)	по выбору подрядчика			м³	3,89	5	мешок по ТУ	по ТУ		S 80,06 м² × толщина; армирование и маяки — по ТУ; л. 66
12	Смесь штукатурная гипсовая для машинного и ручного нанесения по маякам, слой до 10 мм	по выбору подрядчика			м²	198,37	10	мешок по ТУ	по ТУ		пом. 1, 2, 3, 4, 5, 6, 7, 8; расход кг/м² на 1 мм слоя — по ТУ смеси, толщина — по замеру кривизны стен; л. 27, 67, 68
Короба из ГКЛВ											
13	Лист ГКЛВ 12,5 мм, 2500 × 1200 мм, обшивка коробов в 2 слоя	по выбору подрядчика			м²	9,86	10	лист 3,00 м²	4,00 лист		инсталляция пом. 2: 1,76 м²; инсталляция пом. 7: 1,47 м²; короб Ш1 пом. 2: 1,70 м²; площадь × 2 слоя; короб К1 над полом — в спецификации ВК; л. 48, 62–65
14	Профиль стальной оцинкованный 27 × 28 мм: каркас коробов (стойки и направляющие)	по выбору подрядчика			м	24,23	10	хлыст 3 м	9 шт		стойки через 400 мм по свободному периметру + направляющие по полу и потолку; крепёж, лента, шпаклёвка швов — по узлу короба; л. 48, 62–65
Перегородки и облицовки из ГКЛВ											
15	Лист ГКЛВ 12,5 мм, 2500 × 1200 мм: обшивка перегородок и облицовок, 2 слоя на сторону	по выбору подрядчика			м²	14,56	10	лист 3,00 м²	6,00 лист		П-1**, П-2**; площадь стороны × 2 слоя × стороны (проёмы вычтены); предложение, пока П-1**, П-2** не утверждена автором (К-18, К-4); л. 28, 29, 58

Допущения и предложения на листе

Основа листа: размеры сняты со скана плана заказчика по размерным цепочкам, контрольный обмер на объекте не выполнялся (К-13); высота потолка 2700 мм принята: на плане заказчика не указана (К-11); толщины стен приняты: наружные 250 мм, перегородки 150 мм (на плане 85–190 мм) (К-13); разрешённая мощность 15 кВт принята по типовой квартире, технических условий нет (К-14); утолщение стены 190 × 1360 мм и элемент 1470 × 160 мм плана заказчика не определены (К-12); ниши санузла 2 закрыты перегородкой и фальш-стеной: проектное решение, на плане заказчика ниша у входа открыта (К-18); несущие стены не определены: до технического заключения все существующие стены считаются несущими (К-20); окна существующие и сохраняются; подоконная доска и глубина откосов не заданы — приняты, не замерены (К-27); подрайон климата не задан — принят не северный (жилые от 2,5 м) (К-29).

Знак «**» — предложение проектировщика, заказчиком не утверждено (согласовать с заказчиком): ИЗ-2, К-2, К-23: пол пом. 2, 7 — пирог пола: стяжка 33 мм и обмазочная гидроизоляция добавлены разработчиком проекта; артикул изделия не выбран: позиция описана характеристиками («аналог по характеристикам»), артикул выбирается при закупке; К-2, К-23: стены пом. 2, 7 — артикул изделия не выбран: позиция описана характеристиками («аналог по характеристикам»), артикул выбирается при закупке; К-4, К-18: П-1 — проектное решение исполнителя: на плане заказчика ниша у входа открыта в кухню-гостиную; конструкция не утверждена автором (вопрос К-18), положение и размеры сняты со скана (К-13); К-18: П-2 — проектное решение исполнителя: на плане заказчика у наружной стены уступ 660 × 260 мм; конструкция не утверждена автором (вопрос К-18); К-23: пол пом. 1, 3–6, 8, плинтус пом. 1, 3–6, 8, фартук пом. 6 — артикул изделия не выбран: позиция описана характеристиками («аналог по характеристикам»), артикул выбирается при закупке.

Открытые вопросы и конфликты по листу: К-23.

См. лист открытых вопросов (лист 6, записи К-2, К-4; лист 7, записи К-11–К-14, К-18, К-20; лист 8, записи К-23, К-27, К-29; лист 9, запись ИЗ-2).

Изм.	Кол.уч	Лист	№ док.	Подп.	Дата
Разраб.		Кырлан А.С.			13.11.26
Пров.					
ГИП					
Н. контр.					
Утв.					

ГД-2026-003-АИ

Трёхкомнатная квартира

Общая площадь 78,95* м² · * размеры со скана, не замерены (реестр — л. 6–11, К-13)

Дизайн-проект интерьера трёхкомнатной квартиры

Стадия	Лист	Листов
РП	120	132

Спецификация материалов

М б/м

Кырлан Александр Сергеевич

Спецификация материалов (продолжение)

Отделочные материалы: чистое количество, запас, упаковка, к заказу · ГОСТ 21.110-2013

Спецификация материалов (ГОСТ 21.110-2013, форма 1) (продолжение)

Поз.	Наименование и техническая характеристика	Тип, марка, артикул	Код продукции	Поставщик	Ед. изм.	Количество				Масса ед., кг	Примечание
						чистое	запас, %	упаковка	к заказу		
16	Профиль направляющий ПН 100: по потолку и полу, перемычки над проёмами	по выбору подрядчика			м	3,20	10	хлыст 3 м	2 шт		П-1**, П-2**; ПН: шаг и положение стоек — на схеме каркаса; длина стойки равна высоте перегородки, стойки режут между направляющими при монтаже; предложение, пока П-1**, П-2** не утверждена автором (К-18, К-4); л. 28, 29, 58
17	Профиль стоечный ПС 100: стойки через шаг каркаса и короткие над проёмами	по выбору подрядчика			м	9,30	10	хлыст 3 м	4 шт		П-1**, П-2**; ПС: шаг и положение стоек — на схеме каркаса; длина стойки равна высоте перегородки, стойки режут между направляющими при монтаже; предложение, пока П-1**, П-2** не утверждена автором (К-18, К-4); л. 28, 29, 58
18	Профиль усиленный УА 100 (2,0 мм): стойки по краям проёма на полную высоту	по выбору подрядчика			м	5,40	10	хлыст 3 м	2 шт		П-1**, П-2**; УА: шаг и положение стоек — на схеме каркаса; длина стойки равна высоте перегородки, стойки режут между направляющими при монтаже; предложение, пока П-1**, П-2** не утверждена автором (К-18, К-4); л. 28, 29, 58
19	Плита минераловатная звукопоглощающая в полость каркаса, толщина по глубине профиля 100 мм	по выбору подрядчика			м²	2,85	10	упаковка по ТУ	по ТУ		П-1**, П-2**; заполнение принято (К-18): марка и плотность — при закупке; Rw системы нормируют с заполнением; предложение, пока П-1**, П-2** не утверждена автором (К-18, К-4); л. 28, 29, 58
20	Лента уплотнительная самоклеящаяся под профили по потолку, полу и у примыканий к стенам	по выбору подрядчика			м	7,90	10	рулон по ТУ	9,00 м		П-1**, П-2**; по периметру каркаса: потолок, пол без проёма, крайние стойки у примыканий; предложение, пока П-1**, П-2** не утверждена автором (К-18, К-4); л. 28, 29, 58
21	Саморезы для ГКЛ по металлу (по слоям обшивки), дюбели для направляющих — по ТУ изготовителя системы	по выбору подрядчика			м²	14,56		упаковка по ТУ	по ТУ		П-1**, П-2**; расход шт/м² и шаг дюбелей — по ТУ системы; считаются от площади обшивки; предложение, пока П-1**, П-2** не утверждена автором (К-18, К-4); л. 28, 29, 58
22	Шпаклёвка для швов и мест креплений ГКЛВ под плитку (Q1)	по выбору подрядчика			м²	4,43	10	мешок по ТУ	по ТУ		П-1**, П-2**; стороны, облицованные плиткой; сторона под окраску — в позиции шпаклёвки стен; предложение, пока П-1**, П-2** не утверждена автором (К-18, К-4); л. 28, 29, 58
Слаботочные сети											
23	Кабель домофона — тип по системе поставщика	по выбору подрядчика			м	2,90		бухта по ТУ	3,00 м		по лучам от ЩС**, 1 точ., запас 10 % уже в длине; 2 точ. — предложение листа слаботочки (знак «*» на плане); л. 45
24	Кабель коаксиальный RG-6 (75 Ом) к розеткам ТВ	по выбору подрядчика			м	30,30		бухта по ТУ	31,00 м		по лучам от ЩС**, 2 точ., запас 10 % уже в длине; 2 точ. — предложение листа слаботочки (знак «*» на плане); л. 45
25	Кабель U/UTP кат. 6 (LAN, Wi-Fi и камеры по PoE)	по выбору подрядчика			м	62,30		бухта по ТУ	63,00 м		по лучам от ЩС**, 5 точ., запас 10 % уже в длине; 2 точ. — предложение листа слаботочки (знак «*» на плане); л. 45
26	Гофротруба Ø20 для слаботочных линий, отдельно от силовых	по выбору подрядчика			м	86,00		бухта по ТУ	86,00 м		по длине лучей без участков в канале плинтуса (≈ 90 %); л. 45
27	Розетка компьютерная RJ45, кат. 6, с рамкой и подрозетником	по выбору подрядчика			шт	3		шт	3 шт		LAN1–LAN3; серия механизмов — как у розеток и выключателей; л. 40, 41, 45
28	Розетка телевизионная (коаксиальная) с рамкой и подрозетником	по выбору подрядчика			шт	2		шт	2 шт		ТВ1, ТВ2; серия механизмов — как у розеток и выключателей; л. 40, 41, 45
29	Трубка или монитор домофона (поставка домофонной организации)	по выбору подрядчика			шт	1		шт	1 шт		ДФ1; серия механизмов — как у розеток и выключателей; л. 40, 41, 45

Допущения и предложения на листе

Основа листа: размеры сняты со скана плана заказчика по размерным цепочкам, контрольный обмер на объекте не выполнялся (К-13); высота потолка 2700 мм принята: на плане заказчика не указана (К-11); толщины стен приняты: наружные 250 мм, перегородки 150 мм (на плане 85–190 мм) (К-13); разрешённая мощность 15 кВт принята по типовой квартире, технических условий нет (К-14); утолщение стены 190 × 1360 мм и элемент 1470 × 160 мм плана заказчика не определены (К-12); ниши санузла 2 закрыты перегородкой и фальш-стеной: проектное решение, на плане заказчика ниша у входа открыта (К-18); несущие стены не определены: до технического заключения все существующие стены считаются несущими (К-20); окна существующие и сохраняются; подоконная доска и глубина откосов не заданы — приняты, не замерены (К-27); подрайон климата не задан — принят не северный (жилые от 2,5 м) (К-29).

Знак «**» — предложение проектировщика, заказчиком не утверждено (согласовать с заказчиком): ИЗ-2, К-2, К-23: пол пом. 2, 7 — пирог пола: стяжка 33 мм и обмазочная гидроизоляция добавлены разработчиком проекта; артикул изделия не выбран: позиция описана характеристиками («аналог по характеристикам»), артикул выбирается при закупке; ИЗ-9, ИЗ-17, К-7: ЩС — щит слаботочный: место и состав; К-2, К-23: стены пом. 2, 7 — артикул изделия не выбран: позиция описана характеристиками («аналог по характеристикам»), артикул выбирается при закупке; К-4, К-18: П-1 — проектное решение исполнителя: на плане заказчика ниша у входа открыта в кухню-гостиную; конструкция не утверждена автором (вопрос К-18), положение и размеры сняты со скана (К-13); К-18: П-2 — проектное решение исполнителя: на плане заказчика у наружной стены уступ 660 × 260 мм; конструкция не утверждена автором (вопрос К-18); К-23: пол пом. 1, 3–6, 8, плинтус пом. 1, 3–6, 8, фартук пом. 6 — артикул изделия не выбран: позиция описана характеристиками («аналог по характеристикам»), артикул выбирается при закупке.

Открытые вопросы и конфликты по листу: К-23.

См. лист открытых вопросов (лист 6, записи К-2, К-4, К-7; лист 7, записи К-11–К-14, К-18, К-20; лист 8, записи К-23, К-27, К-29; лист 9, записи ИЗ-2, ИЗ-9; лист 11, запись ИЗ-17).

Изм.	Кол.уч	Лист	№ док.	Подп.	Дата
Разраб.		Кырлан А.С.			13.11.26
Пров.					
ГИП					
Н. контр.					
Утв.					

ГД-2026-003-АИ

Трёхкомнатная квартира

Общая площадь 78,95* м² · * размеры со скана, не замерены (реестр — л. 6–11, К-13)

Дизайн-проект интерьера трёхкомнатной квартиры	Стадия	Лист	Листов
	РП	121	132

Спецификация материалов (продолжение)

М б/м

Кырлан Александр Сергеевич

Спецификация материалов (окончание)

Отделочные материалы: чистое количество, запас, упаковка, к заказу · ГОСТ 21.110-2013

Спецификация материалов (ГОСТ 21.110-2013, форма 1) (продолжение)

Поз.	Наименование и техническая характеристика	Тип, марка, артикул	Код продукции	Поставщик	Ед. изм.	Количество				Масса ед., кг	Примечание
						чистое	запас, %	упаковка	к заказу		
30	Щит слаботочный ЩС**: корпус, DIN-рейка, розетки 220 В	по выбору подрядчика			шт	1		шт	1 шт		ЩС**; серия механизмов — как у розеток и выключателей; л. 40, 41, 45
31	Патч-панель, портов не менее 5	по выбору подрядчика			шт	1		шт	1 шт		серия механизмов — как у розеток и выключателей; л. 40, 41, 45
Лакокрасочные материалы											
32	Краска интерьерная акриловая, матовая, класс истирания 1	Farrow & Ball Modern Emulsion No. 30 «Hague Blue»			л	9,26	10	банка 2,5 л	5 банк		38,58 м² × 2 сл. × 0,12 л/м²; пом. 1, 4, 6; л. 67, 68
33	Краска интерьерная акриловая, матовая, класс истирания 1	Farrow & Ball Modern Emulsion No. 241 «Skimming Stone»			л	28,51	10	банка 2,5 л	13 банк		118,77 м² × 2 сл. × 0,12 л/м²; пом. 1, 4, 5, 6, 8; л. 67, 68
34	Краска интерьерная акриловая, глубокоматовая, класс истирания 2	Tikkurila Anti-Reflex 2 V503 «Winter»			л	17,34	10	банка 2,7 л	8 банк		72,23 м² × 2 сл. × 0,12 л/м²; пом. 1 (пот.), 3 (пот.), 4 (пот.), 5 (пот.), 6 (пот.), 8 (пот.); л. 67, 68
35	Краска интерьерная акриловая, матовая, класс истирания 1	Tikkurila Luja 7 V503 «Winter»			л	1,61	10	банка 2,7 л	1 банк		6,72 м² × 2 сл. × 0,12 л/м²; пом. 2 (пот.), 7 (пот.); л. 67, 68
36	Краска интерьерная акриловая, матовая, класс истирания 1	Tikkurila Harmony V503 «Winter»			л	3,54	10	банка 2,7 л	2 банк		14,74 м² × 2 сл. × 0,12 л/м²; пом. 3; л. 67, 68
37	Шпаклёвка финишная полимерная под окраску (стены и потолки, Q3)	по выбору подрядчика			м²	251,04	10	ведро по ТУ	по ТУ		расход кг/м² на слой — по ТУ; л. 67, 68
38	Грунтовка акриловая глубокого проникновения, 2 слоя	по выбору подрядчика			м²	284,60	10	канистра по ТУ	по ТУ		расход л/м² — по ТУ; л. 67, 68
Погонажные изделия и потолки											
39	Плинтус напольный МДФ под покраску, h=80 мм, крепление к стене	аналог: плинтус МДФ под покраску 80×16			м.п.	70,34	10	хлыст 2,4 м	33 шт		пом. 1, 3, 4, 5, 6, 8; длина хлыста — по артикулу; л. 67, 68
40	Потолок подвесной ГКЛ/ГКЛВ по каркасу Knauf П113: листы, профили, подвесы, лента, шпаклёвка швов	Knauf П113			м²	77,10		комплект	по л. потолков		площадь — по ведомости потолков; число листов, профилей и подвесов — по шагам каркаса на листе потолков; л. 59–61

Примечания

1. Чистое количество — из ведомости объёмов работ и раскладки плитки; запас — отдельной графой (доска — по ведомости отделки, плитка, краска и плинтус — 10 %); «к заказу» — с запасом и кратно упаковке.
2. Плитка — штуками по раскладке, запас на каждую поверхность. Калибр (рабочий размер) и тон — одной партией на помещение, калибр указать при заказе и сверить с раскладкой до укладки.
3. Краска — 0,12 л/м² на слой (середина вилки 0,10–0,15 л/м²) по фактической площади окраски из ведомости отделки; колеровка одной партией.
4. «По ТУ» — расход задаёт производитель выбранного продукта; количество к заказу — после выбора марки.
5. Поз. 1, 3, 4, 5, 6, 39 заданы характеристиками («аналог:»): марку, артикул и поставщика согласовать с заказчиком до закупки, без артикула не заказывать.
6. Штукатурная смесь — на ту же площадь, что строка ВОР «Штукатурка стен» (198,37 м²): площадь одна, расход смеси задаёт производитель.
7. Коробы инсталляции и стояков: ГКЛВ в 2 слоя и профиль 27 × 28 мм считаются по свободным граням коробов (источник — раскладка плиточника и шахты в данных); короб К1 над полом — в спецификации ВК.
8. Потолки ГКЛ: в этой спецификации — площадь системы П113; число листов, профилей и подвесов — по шагам каркаса на листе потолков (подвесы через 1000, несущие через 500, основные через 1200 мм), схема каркаса не выпущена. Сантехника, светильники и мебель — по своим спецификациям.

Допущения и предложения на листе

Основа листа: размеры сняты со скана плана заказчика по размерным цепочкам, контрольный обмер на объекте не выполнялся (К-13); высота потолка 2700 мм принята: на плане заказчика не указана (К-11); толщины стен приняты: наружные 250 мм, перегородки 150 мм (на плане 85–190 мм) (К-13); разрешённая мощность 15 кВт принята по типовой квартире, технических условий нет (К-14); утолщение стены 190 × 1360 мм и элемент 1470 × 160 мм плана заказчика не определены (К-12); ниши санузла 2 закрыты перегородкой и фальш-стеной: проектное решение, на плане заказчика ниша у входа открыта (К-18); несущие стены не определены: до технического заключения все существующие стены считаются несущими (К-20); окна существующие и сохраняются; подоконная доска и глубина откосов не заданы — приняты, не замерены (К-27); подрайон климата не задан — принят не северный (жилые от 2,5 м) (К-29).

Знак «**» — предложение проектировщика, заказчиком не утверждено (согласовать с заказчиком): ИЗ-2, К-2, К-23: пол пом. 2, 7 — пирог пола: стяжка 33 мм и обмазочная гидроизоляция добавлены разработчиком проекта; артикул изделия не выбран: позиция описана характеристиками («аналог по характеристикам»), артикул выбирается при закупке; ИЗ-9, ИЗ-17, К-7: ЩС — щит слаботочный: место и состав; К-2, К-23: стены пом. 2, 7 — артикул изделия не выбран: позиция описана характеристиками («аналог по характеристикам»), артикул выбирается при закупке; К-23: пол пом. 1, 3–6, 8, плинтус пом. 1, 3–6, 8, фартук пом. 6 — артикул изделия не выбран: позиция описана характеристиками («аналог по характеристикам»), артикул выбирается при закупке.

Открытые вопросы и конфликты по листу: К-23.

См. лист открытых вопросов (лист 6, записи К-2, К-7; лист 7, записи К-11–К-14, К-18, К-20; лист 8, записи К-23, К-27, К-29; лист 9, записи ИЗ-2, ИЗ-9; лист 11, запись ИЗ-17).

Изм.	Кол.уч	Лист	№ док.	Подп.	Дата				
Разраб.		Кырлан А.С.			13.11.26				
Пров.									
ГИП									
Н. контр.									
Утв.									

ГД-2026-003-АИ

Трёхкомнатная квартира

Общая площадь 78,95* м² · * размеры со скана, не замерены (реестр — л. 6–11, К-13)

Дизайн-проект интерьера трёхкомнатной квартиры	Стадия	Лист	Листов
	РП	122	132
Спецификация материалов (окончание) М б/м	**Кырлан Александр Сергеевич**		

Смета ориентировочная

ПРЕДВАРИТЕЛЬНО · не для производства работ · открыто пунктов: 28 (реестр — л. 6–11)

Работы, материалы, оборудование, услуги и резерв · цены — ориентир по открытым прайсам, не коммерческое предложение

Сводная смета (прайсы собраны 21.09.2026, часть расценок сверена повторно 06.10.2026 и 08.11.2026, Москва)

№	Наименование работ, материалов, услуг	Ед. изм.	Кол-во	Цена за ед., ₽	Стоимость, ₽			Чей подряд	Срок поставки, дн.	Основание	Источник цены
					план	факт	разница				
Работы — по ведомости объёмов работ											
1	Демонтаж и черновые работы (без 8 поз. по КП)	раздел	1		282 510			бригада		ВОР, поз. 1–15; л. 116–119	по ВОР
2	Инженерные системы (без 12 поз. по КП)	раздел	1		201 811			бригада		ВОР, поз. 16–39; л. 116–119	по ВОР
3	Чистовые работы (без 2 поз. по КП)	раздел	1		608 862			бригада, поставщик		ВОР, поз. 40–58; л. 116–119	по ВОР
Материалы — по спецификации материалов											
4	Инженерная доска	м²	70,40	4 513	317 715			поставщик		спецификация, поз. 1	Ц7
5	Керамогранит 600×600 мм	м²	9,72	1 800	17 496			поставщик		спецификация, поз. 3	Ц6
6	Керамогранит 600×1200, 1200×600 мм	м²	70,56	3 500	246 960			поставщик		спецификация, поз. 4, 5, 6	Ц6
7	Клей плиточный цементный класса C2 TE S1	меш.	13	1 800	23 400			поставщик		спецификация, поз. 7	Ц7
8	Затирка цементная класса CG2WA	упак.	2	1 000	2 000			поставщик		спецификация, поз. 8	Ц7
9	Краска Farrow & Ball Modern Emulsion, банка 2,5 л	банк	18	5 800	104 400			поставщик		спецификация, поз. 32, 33	Ц7
10	Краска Tikkurila (Anti-Reflex 2, Luja 7, Harmony), банка 2,7 л	банк	11	3 510	38 610			поставщик		спецификация, поз. 34, 35, 36	Ц6
11	Плинтус напольный МДФ под покраску	шт	33	368	12 144			поставщик		спецификация, поз. 39	Ц7
12	Прочие материалы с расходом по ТУ (клей для доски, гидроизоляция, демпферная лента, смесь для стяжки, смесь штукатурная гипсовая для машинного и ручного нанесения по маякам, лист гклв 12, профиль стальной оцинкованный 27 × 28 мм: каркас коробов (стойки и направляющие), ГКЛВ перегородок, профиль ПН, профиль ПС, профиль УА, минвата в каркас, лента уплотнительная, крепёж каркаса, шпаклёвка швов, кабель слаботочки, гофра слаботочки, изделия слаботочки, шпаклёвка, грунтовка, каркас и ГКЛ потолков)	компл	1	по КП				поставщик		спецификация, поз. 2, 9, 10, 11, 12, 13, 14, 15, 16, 17, 18, 19, 20, 21, 22, 23, 24, 25, 26, 27, 28, 29, 30, 31, 37, 38, 40	
Оборудование и мебель — поставка по спецификациям											
13	Кухонный гарнитур по проекту кухни, изготовление и монтаж (4–8 нед.)	компл	1	по КП				поставщик	не задан; ориентир 4–8 нед. от замера	л. 81–83	
14	Двери скрытого монтажа с коробом под покраску, поставка	шт	5	по КП				поставщик	не задан; ориентир ≈ 30 дн.	л. 30	

Допущения и предложения на листе

Основа листа: размеры сняты со скана плана заказчика по размерным цепочкам, контрольный обмер на объекте не выполнялся (К-13); высота потолка 2700 мм принята: на плане заказчика не указана (К-11); толщины стен приняты: наружные 250 мм, перегородки 150 мм (на плане 85–190 мм) (К-13); разрешённая мощность 15 кВт принята по типовой квартире, технических условий нет (К-14); утолщение стены 190 × 1360 мм и элемент 1470 × 160 мм плана заказчика не определены (К-12); ниши санузла 2 закрыты перегородкой и фальш-стеной: проектное решение, на плане заказчика ниша у входа открыта (К-18); несущие стены не определены: до технического заключения все существующие стены считаются несущими (К-20); окна существующие и сохраняются; подоконная доска и глубина откосов не заданы — приняты, не замерены (К-27); подрайон климата не задан — принят не северный (жилые от 2,5 м) (К-29).

Открытые вопросы и конфликты по листу: К-23, К-28.

См. лист открытых вопросов (лист 7, записи К-11–К-14, К-18, К-20; лист 8, записи К-23, К-27–К-29).

Изм.	Кол.уч	Лист	№ док.	Подп.	Дата
Разраб.		Кырлан А.С.			13.11.26
Пров.					
ГИП					
Н. контр.					
Утв.					

ГД-2026-003-АИ

Трёхкомнатная квартира

Общая площадь 78,95* м² · * размеры со скана, не замерены (реестр — л. 6–11, К-13)

Дизайн-проект интерьера трёхкомнатной квартиры

Стадия	Лист	Листов
РП	123	132

Смета ориентировочная

М б/м

Кырлан Александр Сергеевич

Смета ориентировочная (окончание)

ПРЕДВАРИТЕЛЬНО · не для производства работ · открыто пунктов: 28 (реестр — л. 6–11)

Работы, материалы, оборудование, услуги и резерв · цены — ориентир по открытым прайсам, не коммерческое предложение

Сводная смета (прайсы собраны 21.09.2026, часть расценок сверена повторно 06.10.2026 и 08.11.2026, Москва) (продолжение)

№	Наименование работ, материалов, услуг	Ед. изм.	Кол-во	Цена за ед., ₽	Стоимость, ₽			Чей подряд	Срок поставки, дн.	Основание	Источник цены
					план	факт	разница				
15	Оборудование заказчика слаботочных сетей: точка доступа wi-fi — 2 шт; коммутатор — 1 шт	компл	1	по КП				заказчик		л. 40, 41	
16	Сантехника, светильники, мебель и предметы интерьера	компл	1	по КП				поставщик		л. 56; л. 57; л. 86; л. 33–36	
Прочие работы и услуги											
17	Вынос и вывоз строительного мусора	м³		по факту				бригада		после демонтажа	
18	Подъём материалов на этаж (лифтом или вручную — по договору)	т		по факту				бригада		по массе поставки	
19	Доставка чистовых материалов, 10 % от поставки			10 %	76 273			поставщик		от суммы материалов	
20	Уборка после ремонта	м²	78,95	по факту				бригада		S квартиры	
	Итого работы				**1 093 183**						
	Итого материалы				**762 725**						
	Итого прочие услуги				**76 273**						
	Резерв на непредвиденные работы и материалы, 15 %				**289 827**						
	ВСЕГО ориентировочно (без оборудования и позиций по КП)				**2 222 008**						

Примечания

1. Смета ориентировочная, не коммерческое предложение: объёмы — из ведомости объёмов работ и спецификации материалов, цены — нижняя граница открытых прайсов Москвы (прайсы собраны 21.09.2026, часть расценок сверена повторно 06.10.2026 и 08.11.2026); перед договором цены подтвердить у подрядчика и поставщиков.
2. Источники цен: Ц1 — Домашний мастерок: прайс на отделочные работы, 2026; Ц2 — Домашний мастерок: прайс на плиточные работы, 2026; Ц3 Домашний мастерок: прайс на электромонтажные работы, 2026; Ц4 — Профи ремонтник: штукатурно-малярные работы; Ц5 — Profi.ru: укладка керамогранита на стены, Москва 2026; Ц6 — knowledge/spec-materials.md, разд. 1 и 3: ориентир по сегментам; Ц7 — Розница Москвы, 09.2026: Леманa ПРО, KGSnab, официальный дилер Farrow & Ball.
3. Повторная сверка с прайсом: 06.10.2026 — перегородка в 2 слоя с усиленным каркасом, облицовка в 2 слоя; 08.11.2026 — гофра слаботочки с затяжкой; остальные расценки — по прайсам, собранным 21.09.2026.
4. В итог не вошли позиции «по КП» и «по факту»: оборудование и мебель, двери, материалы с расходом по ТУ, вывоз мусора, подъём и уборка.
5. В разделе 1 учтены работы по П-1** и П-2** — 9 354 ₽ (расценка Ц1 за м² конструкции; П-1** — по расценке «усиленный каркас» 2 700 ₽/м² вместо 1 500 ₽/м²: шаг стоек 400 мм или проём с обрамлением УА): это предложение проектировщика, не утверждённое автором (К-18, К-4); если конструкции не будет, строки и материалы к ним снимаются, санузел 2 пересчитывается. Обрамление проёма УА, заполнение, профиль и обшивка — материалы «по ТУ», в итог не входят.
6. Доставка — 10 % от материалов, резерв — 15 % (частный ремонт 10–20 %) отдельными строками, в количествах не спрятаны. Графы «факт» и «разница» заполняются по актам.

Допущения и предложения на листе

Основа листа: размеры сняты со скана плана заказчика по размерным цепочкам, контрольный обмер на объекте не выполнялся (К-13); высота потолка 2700 мм принята: на плане заказчика не указана (К-11); толщины стен приняты: наружные 250 мм, перегородки 150 мм (на плане 85–190 мм) (К-13); разрешённая мощность 15 кВт принята по типовой квартире, технических условий нет (К-14); утолщение стены 190 × 1360 мм и элемент 1470 × 160 мм плана заказчика не определены (К-12); ниши санузла 2 закрыты перегородкой и фальш-стеной: проектное решение, на плане заказчика ниша у входа открыта (К-18); несущие стены не определены: до технического заключения все существующие стены считаются несущими (К-20); окна существующие и сохраняются; подоконная доска и глубина откосов не заданы — приняты, не замерены (К-27); подрайон климата не задан — принят не северный (жилые от 2,5 м) (К-29).

Знак «**» — предложение проектировщика, заказчиком не утверждено (согласовать с заказчиком): К-4, К-18: П-1 — проектное решение исполнителя: на плане заказчика ниша у входа открыта в кухню-гостиную; конструкция не утверждена автором (вопрос К-18), положение и размеры сняты со скана (К-13); К-18: П-2 — проектное решение исполнителя: на плане заказчика у наружной стены уступ 660 × 260 мм; конструкция не утверждена автором (вопрос К-18).

Открытые вопросы и конфликты по листу: К-23, К-28.

См. лист открытых вопросов (лист 6, запись К-4; лист 7, записи К-11–К-14, К-18, К-20; лист 8, записи К-23, К-27–К-29).

Изм.	Кол.уч	Лист	№ док.	Подп.	Дата
Разраб.		Кырлан А.С.			13.11.26
Пров.					
ГИП					
Н. контр.					
Утв.					

ГД-2026-003-АИ

Трёхкомнатная квартира

Общая площадь 78,95* м² · * размеры со скана, не замерены (реестр — л. 6–11, К-13)

Дизайн-проект интерьера трёхкомнатной квартиры

Стадия	Лист	Листов
РП	124	132

Смета ориентировочная (окончание)

М б/м

Кырлан Александр Сергеевич

выпуск 13.11.2026 № 6f3a8abb2c · стр. 134 из 157

Смета проекта: этапы, помещения, итог

Весь проект: ремонт, мебель, свет, техника, декор · вилка «от … до …» · позиции «по КП» посчитаны отдельно · цены — ориентир, не оферта

Смета проекта: весь проект по категориям (прайсы собраны 21.09.2026, часть расценок сверена повторно 06.10.2026 и 08.11.2026)

Категория	Позиций	С ценой	По КП	Сумма по позициям с ценой, ₽
Ремонт: работы	58	36	22	1 093 183
Ремонт: материалы отделки и черновые	36	13	23	762 725
Электрика: кабель, механизмы, щит	40	0	40	
Сантехника: приборы, трубы, арматура	38	0	38	
Доставка и услуги	4	1	3	76 273
Мебель (включая кухню)	22	0	22	
Свет: светильники и ленты	54	0	54	
Техника	7	0	7	
Декор и текстиль	63	0	63	
ИТОГО по позициям с ценой (цены — нижняя граница открытых прайсов)	**322**	**50**	**272**	**1 932 181**
Резерв на непредвиденные работы и материалы, 15 % от ремонта				289 827
ВЕСЬ ПРОЕКТ — вилка «от … до …», ₽				**1 932 181 … 2 222 008**
Позиции «по КП» — цена не названа, в итог НЕ входят: работы — 22; материалы отделки и черновые — 23; электрика: кабель, механизмы, щит — 40; сантехника: приборы, трубы, арматура — 38; доставка и услуги — 3; мебель (включая кухню) — 22; свет: светильники и ленты — 54; техника — 7; декор и текстиль — 63			**272**	**итог выше на их цену**

По этапам

Этап	Поз.	С ценой	Сумма, ₽
Демонтаж и черновые работы (работы)	15	7	282 510
Инженерные системы (работы)	24	12	201 811
Чистовые работы (работы)	19	17	608 862
Черновые материалы (смеси, ГКЛ, гидроизоляция)	20	2	25 400
Электрика: кабель, механизмы, щит, слаботочка	40	0	
Сантехника: приборы, трубы, арматура	38	0	
Чистовые материалы (отделка, двери)	16	11	737 325
Доставка и услуги	4	1	76 273
Резерв на непредвиденное, 15 %	1	1	289 827
Итого ремонт (с резервом)			**2 222 008**

По помещениям

Помещение	Работы, ₽	Материалы, ₽	Всего, ₽
Общее по объекту (без привязки к помещению)	54 834		54 834
1. Спальня 1	192 015	123 598	315 613
2. Ванная	118 765	143 826	262 591
3. Гардеробная	36 273	17 876	54 149
4. Спальня 2	153 376	92 449	245 825
5. Прихожая	95 738	53 458	149 196
6. Кухня-гостиная	302 351	207 152	509 503
7. Санузел 2	77 295	97 001	174 296
8. Коридор	62 536	27 365	89 901
Доставка и услуги			76 273
Резерв 15 %			289 827
Итого ремонт (с резервом)			**2 222 008**

Допущения и предложения на листе

Основа листа: размеры сняты со скана плана заказчика по размерным цепочкам, контрольный обмер на объекте не выполнялся (К-13); высота потолка 2700 мм принята: на плане заказчика не указана (К-11); толщины стен приняты: наружные 250 мм, перегородки 150 мм (на плане 85–190 мм) (К-13); разрешённая мощность 15 кВт принята по типовой квартире, технических условий нет (К-14); утолщение стены 190 × 1360 мм и элемент 1470 × 160 мм плана заказчика не определены (К-12); ниши санузла 2 закрыты перегородкой и фальш-стеной: проектное решение, на плане заказчика ниша у входа открыта (К-18); несущие стены не определены: до технического заключения все существующие стены считаются несущими (К-20); окна существующие и сохраняются; подоконная доска и глубина откосов не заданы — приняты, не замерены (К-27); подрайон климата не задан — принят не северный (жилые от 2,5 м) (К-29).

См. лист открытых вопросов (лист 7, записи К-11–К-14, К-18, К-20; лист 8, записи К-27, К-29).

Изм.	Кол.уч	Лист	№ док.	Подп.	Дата
Разраб.		Кырлан А.С.			13.11.26
Пров.					
ГИП					
Н. контр.					
Утв.					

ГД-2026-003-АИ

Трёхкомнатная квартира

Общая площадь 78,95* м² · * размеры со скана, не замерены (реестр — л. 6–11, К-13)

Дизайн-проект интерьера трёхкомнатной квартиры

Стадия	Лист	Листов
РП	125	132

Смета проекта: этапы, помещения, итог

М б/м

Кырлан Александр Сергеевич

выпуск 13.11.2026 № 6f3a8abb2c · стр. 135 из 157

Смета проекта: этапы, помещения, итог (продолжение)

ПРЕДВАРИТЕЛЬНО · не для производства работ · открыто пунктов: 28 (реестр — л. 6–11)

Весь проект: ремонт, мебель, свет, техника, декор · вилка «от … до …» · позиции «по КП» посчитаны отдельно · цены — ориентир, не оферта

Работы по этапам с расценками (ориентир)

№	Работа	Ед.	Объём	Расценка, ₽	Сумма, ₽	Расценка	Чей подряд
1. Демонтаж и черновые работы — работы, ориентир по открытым прайсам							
1	Демонтаж существующего покрытия пола до основания	м²	78,95	по КП			бригада
2	Демонтаж существующей отделки стен до основания	м²	205,65	по КП			бригада
3	Демонтаж существующей отделки потолка до основания	м²	78,95	по КП			бригада
4	Демонтаж существующих дверных блоков	шт	6,00	по КП			бригада
5	Демонтаж существующих сантехприборов и электрооборудования (если есть)	компл		по КП			бригада
6	Монтаж каркасной перегородки П-1** (С112): каркас ПС усиленный через 400 мм, ГКЛВ в 2 слоя с каждой стороны, обрамление проёма профилем УА; предложение, пока П-1** не утверждена автором (К-18, К-4)	м²	2,85	2 700	7 695	Ц1	бригада
7	Облицовка (фальш-стена) П-2**: ГКЛВ в 2 слоя по раме инсталляции под плитку; предложение, пока П-2** не утверждена автором (К-18)	м²	1,58	1 050	1 659	Ц1	бригада
8	Заполнение каркаса П-1** минераловатной плитой (звукоизоляция, Rw 51 дБ); предложение, пока П-1** не утверждена автором (К-18, К-4)	м²	2,85	по КП			бригада
9	Шпаклёвка швов ГКЛВ П-1** под плитку (Q1), сторона санузла; предложение, пока П-1** не утверждена автором (К-18, К-4)	м²	2,85	по КП			бригада
10	Шпаклёвка швов ГКЛВ П-2** под плитку (Q1), сторона санузла; предложение, пока П-2** не утверждена автором (К-18)	м²	1,58	по КП			бригада
11	Устройство стяжки: стяжка ЦПС М200, 50 мм	м²	80,06	530	42 432	Ц1	бригада
12	Гидроизоляция обмазочная, 2 слоя: пол, стены на 200 мм, зоны замачивания	м²	18,15	450	8 167	Ц1	бригада
13	Штукатурка стен по маякам, до 10 мм	м²	198,37	530	105 136	Ц1	бригада
14	Штукатурка оконных откосов шириной до 200 мм	м²	3,28	540	1 771	Ц4	бригада
15	Потолок ГКЛ по каркасу П113, 1 слой	м²	77,10	1 500	115 650	Ц1	бригада
2. Инженерные системы — работы, ориентир по открытым прайсам							
16	Прокладка кабеля ВВГнг(А)-LS по группам щита: за потолком и в штробах стен (штробы — только после технического заключения, см. строку «Штробы в стенах»)	м	493,50	60	29 610	Ц3	бригада
17	Прокладка слаботочной линии: Кабель домофона — тип по системе поставщика, отдельно от силовых	м	2,90	по КП			бригада
18	Прокладка слаботочной линии: Кабель коаксиальный RG-6 (75 Ом) к розеткам ТВ, отдельно от силовых	м	30,30	по КП			бригада
19	Прокладка слаботочной линии: Кабель U/UTP кат. 6 (LAN, Wi-Fi и камеры по PoE), отдельно от силовых	м	62,30	по КП			бригада
20	Прокладка гофротрубы Ø20 для слаботочных линий, отдельно от силовых	м	86,00	140	12 040	Ц3	бригада
21	Сборка слаботочного щита ЩС**: корпус, патч-панель, подключение линий и питания 220 В; коммутатор и точки доступа — оборудование заказчика	шт	1,00	по КП			бригада
22	Электроточка: подрозетник в бетоне, розетка, выключатель, вывод	шт	67,00	950	63 650	Ц3	бригада
23	Штробы в стенах под спуски кабеля к точкам — выполняются только после технического заключения о несущих стенах	м	105,95	по КП			бригада
24	Установка встраиваемого точечного светильника	шт	39,00	750	29 250	Ц3	бригада
25	Монтаж светильника: потолочного, подвесного, настенного	шт	10,00	1 200	12 000	Ц3	бригада
26	Монтаж LED-ленты в алюминиевый профиль	м	54,70	230	12 581	Ц3	бригада
27	Установка блока питания LED в доступном месте (люк, шкаф)	шт	5,00	570	2 850	Ц3	бригада
28	Установка автономного пожарного извещателя	шт	6,00	по КП			бригада
29	Сборка щита: установка автоматов и АВДТ групп, вводного автомата	шт	15,00	230	3 450	Ц3	бригада
30	Установка вводного УЗО	шт	1,00	380	380	Ц3	бригада

Допущения и предложения на листе

Основа листа: размеры сняты со скана плана заказчика по размерным цепочкам, контрольный обмер на объекте не выполнялся (К-13); высота потолка 2700 мм принята: на плане заказчика не указана (К-11); толщины стен приняты: наружные 250 мм, перегородки 150 мм (на плане 85–190 мм) (К-13); разрешённая мощность 15 кВт принята по типовой квартире, технических условий нет (К-14); утолщение стены 190 × 1360 мм и элемент 1470 × 160 мм плана заказчика не определены (К-12); ниши санузла 2 закрыты перегородкой и фальш-стеной: проектное решение, на плане заказчика ниша у входа открыта (К-18); несущие стены не определены: до технического заключения все существующие стены считаются несущими (К-20); окна существующие и сохраняются; подоконная доска и глубина откосов не заданы — приняты, не замерены (К-27); подрайон климата не задан — принят не северный (жилые от 2,5 м) (К-29).

Знак «**» — предложение проектировщика, заказчиком не утверждено (согласовать с заказчиком): ИЗ-9, ИЗ-17, К-7: ЩС — щит слаботочный: место и состав; К-4, К-18: П-1 — проектное решение исполнителя: на плане заказчика ниша у входа открыта в кухню-гостиную; конструкция не утверждена автором (вопрос К-18), положение и размеры сняты со скана (К-13); К-18: П-2 — проектное решение исполнителя: на плане заказчика у наружной стены уступ 660 × 260 мм; конструкция не утверждена автором (вопрос К-18).

См. лист открытых вопросов (лист 6, записи К-4, К-7; лист 7, записи К-11–К-14, К-18, К-20; лист 8, записи К-27, К-29; лист 9, запись ИЗ-9; лист 11, запись ИЗ-17).

Изм.	Кол.уч	Лист	№ док.	Подп.	Дата
Разраб.		Кырлан А.С.			13.11.26
Пров.					
ГИП					
Н. контр.					
Утв.					

ГД-2026-003-АИ

Трёхкомнатная квартира

Общая площадь 78,95* м² · * размеры со скана, не замерены (реестр — л. 6–11, К-13)

Дизайн-проект интерьера трёхкомнатной квартиры

Стадия	Лист	Листов
РП	126	132

Смета проекта: этапы, помещения, итог (продолжение)

М б/м

Кырлан Александр Сергеевич

Смета проекта: этапы, помещения, итог (окончание)

Весь проект: ремонт, мебель, свет, техника, декор · вилка «от … до …» · позиции «по КП» посчитаны отдельно · цены — ориентир, не оферта

Работы по этапам с расценками (ориентир) (продолжение)

№	Работа	Ед.	Объём	Расценка, ₽	Сумма, ₽	Расценка	Чей подряд
31	Монтаж инсталляции, установка подвесного унитаза и кнопки смыва	шт	2,00	10 500	21 000	Ц1	бригада
32	Короб инсталляции: каркас и обшивка ГКЛВ в 2 слоя, ревизионный доступ к смыву	шт	2,00	по КП			бригада
33	Короб стояков Ш1 248 × 459 мм (внутренний 195 × 406): каркас и обшивка ГКЛВ в 2 слоя, ревизионный люк 300 × 400	м²	1,70	по КП			бригада
34	Короб К1 над чистым полом: каркас и обшивка ГКЛВ под плитку (материалы — в спецификации ВК)	м	2,17	по КП			бригада
35	Установка ванны с сифоном	шт	1,00	6 000	6 000	Ц1	бригада
36	Установка умывальника (мойки) с сифоном и смесителем	шт	3,00	3 000	9 000	Ц1	бригада
37	Установка душевого поддона с трапом, ограждения	шт	1,00	по КП			бригада
38	Подключение стиральной (посудомоечной) машины к ВК	шт	2,00	по КП			бригада
39	Установка радиатора с узлом подключения и терморегулятором	шт	4,00	по КП			бригада
3. Чистовые работы — работы, ориентир по открытым прайсам							
40	Облицовка стен керамогранитом 600×1200 на клею	м²	28,38	2 500	70 950	Ц5	бригада
41	Облицовка короба инсталляции (ГКЛВ) керамогранитом: лицо, боковины, полка	м²	4,88	2 500	12 200	Ц5	бригада
42	Облицовка фартука керамогранитом 1200×600	м²	1,85	2 400	4 440	Ц2	бригада
43	Укладка керамогранита на пол, 600×600, на клею	м²	14,28	1 800	25 704	Ц2	бригада
44	Затирка швов керамогранита	м²	48,96	150	7 344	Ц2	бригада
45	Грунтование стен, 2 слоя (под штукатурку и под отделку)	м²	205,65	96	19 742	Ц4	бригада
46	Шпаклёвка стен под окраску, 2 слоя (старт и финиш), уровень Q3	м²	172,09	750	129 068	Ц1	бригада
47	Грунтование и шпаклёвка оконных откосов, 2 слоя	м	18,19	300	5 457	Ц4	бригада
48	Грунтование потолка, 2 слоя	м²	78,95	96	7 579	Ц4	бригада
49	Шпаклёвка потолка под окраску, 2 слоя, уровень Q3	м²	78,95	950	75 003	Ц1	бригада
50	Окраска потолка водно-дисперсионной краской, 2 слоя	м²	78,95	360	28 422	Ц1	бригада
51	Окраска стен водно-дисперсионной краской, 2 слоя	м²	209,43	300	62 829	Ц1	бригада
52	Окраска оконных откосов, 2 слоя	м	18,19	120	2 183	Ц4	бригада
53	Укладка инженерной доски на клей	м²	65,78	1 200	78 936	Ц1	бригада
54	Установка плинтуса МДФ h=80 мм	м	70,34	450	31 653	Ц1	бригада
55	Окраска плинтуса в тоне No. 241, 2 слоя	м	70,34	300	21 102	Ц1	бригада
56	Монтаж дверей скрытого монтажа под покраску (поставщик дверей)	шт	5,00	5 250	26 250	Ц1	поставщик
57	Входная дверь, поставка с монтажом и откосами	шт	1,00	по КП			поставщик
58	Монтаж телевизора C12** на кронштейн, скрытая прокладка HDMI и питания (штроба, трубка), подключение акустики	шт	2,00	по КП			бригада
4. Прочие работы и услуги — работы, ориентир по открытым прайсам							
59	Кухонный гарнитур по проекту кухни, изготовление и монтаж (4–8 нед.)	компл	1,00	по КП			поставщик
	Итого работы (позиции с расценкой)				**1 093 183**		

Примечания

1. Итог «ВЕСЬ ПРОЕКТ» — не прогноз, а сумма того, у чего есть цена: ремонт (работы и материалы по смете сметчика), мебель, свет, техника и декор — по ценам из данных проекта. Позиции без цены названы «по КП» (272 шт.) и в итог не входят: пока цена не названа, итог выше напечатанного.
2. Вилка: «от» — сумма по позициям с ценой по нижней границе открытых прайсов (прайсы собраны 21.09.2026, часть расценок сверена повторно 06.10.2026 и 08.11.2026, Москва); «до» — «от» плюс резерв на непредвиденное (15 % от ремонта; частный ремонт 10–20 %).
3. Работы — ориентир по прайсам подрядчиков, не договорная цена: расценку называет бригада после контрольного обмера. Материалы — по «Смете материалов с ценами» (следующий лист).
4. Разбивка по помещениям — доли: общая закупка делится пропорционально площади (длине, числу), по которой считается позиция; работы — по объёму строки в помещении. Сумма по помещениям, по этапам и по категориям одна и та же.
5. Источники расценок и цен: Ц1 — Домашний мастерок: прайс на отделочные работы, 2026; Ц2 — Домашний мастерок: прайс на плиточные работы, 2026; Ц3 — Домашний мастерок: прайс на электромонтажные работы, 2026; Ц4 — Профи ремонтник: штукатурно-малярные работы; Ц5 — Profi.ru: укладка керамогранита на стены, Москва 2026; Ц6 — справочник материалов: ориентир по сегментам; Ц7 — Розница Москвы, 09.2026: Лемана ПРО, KGSnab, официальный дилер Farrow & Ball.
6. Оборудование «по КП» из сметы сметчика (кухня и др.): 1 поз. — в позиции «по КП» мебели и техники.

Допущения и предложения на листе. Знак «**» предложено (согласовать). См. лист открытых вопросов (листы 6–11).

Изм.	Кол.уч	Лист	№ док.	Подп.	Дата
Разраб.		Кырлан А.С.			13.11.26
Пров.					
ГИП					
Н. контр.					
Утв.					

ГД-2026-003-АИ

Трёхкомнатная квартира

Общая площадь 78,95* м² · * размеры со скана, не замерены (реестр — л. 6–11, К-13)

Дизайн-проект интерьера трёхкомнатной квартиры

Стадия	Лист	Листов
РП	127	132

Смета проекта: этапы, помещения, итог (окончание)
М б/м

Кырлан Александр Сергеевич

Смета материалов с ценами

ПРЕДВАРИТЕЛЬНО · не для производства работ · открыто пунктов: 28 (реестр — л. 6–11)

Все материалы с количеством, запасом, упаковкой, ценой и сроком · цены — ориентир по открытым прайсам, не оферта · работы не входят

Смета материалов с ценами

№	Позиция	Ед.	Нетто	Запас	С запасом	К закупке (упаковка)	Цена за ед., ₽	Сумма, ₽	Заказать заранее	Доп.
Чистовая отделка — позиций 16, с ценой 11, итого 737 325 ₽										
Покрытия полов и облицовка										
1	Инженерная доска (дуб натуральный, рабочий слой 4 мм, эмиссия E1, прямая укладка)	м²	65,78	7 %	70,38	70,40 м²	4 513 / м²	317 715		1, 8
2	Керамогранит 600×600 мм под травертин — керамогранит под травертин	шт	24	13 %	27	27 шт · коробка	1 800 / м²	17 496		1, 8
3	Керамогранит 600×1200 мм под травертин — керамогранит под травертин	шт	67	18 %	79	79 шт · коробка	3 500 / м²	199 080		1, 8
4	Керамогранит 600×1200 мм ректифицированный под травертин, матовый — керамогранит ректифицированный под травертин, матовый	шт	12	17 %	14	14 шт · коробка	3 500 / м²	35 280		1, 8
5	Керамогранит 1200×600 мм под травертин, матовый — керамогранит под травертин, матовый	шт	4	25 %	5	5 шт · коробка	3 500 / м²	12 600		1, 8
Лакокрасочные материалы										
6	Краска интерьерная акриловая, матовая, класс истирания 1 — Farrow & Ball Modern Emulsion No. 30 «Hague Blue»	л	9,26	10 %	10,19	5 банка · банка 2,5 л	5 800 / банк	29 000		8
7	Краска интерьерная акриловая, матовая, класс истирания 1 — Farrow & Ball Modern Emulsion No. 241 «Skimming Stone»	л	28,51	10 %	31,36	13 банка · банка 2,5 л	5 800 / банк	75 400		8
8	Краска интерьерная акриловая, глубокоматовая, класс истирания 2 — Tikkurila Anti-Reflex 2 V503 «Winter»	л	17,34	10 %	19,07	8 банка · банка 2,7 л	3 510 / банк	28 080		8
9	Краска интерьерная акриловая, матовая, класс истирания 1 — Tikkurila Luja 7 V503 «Winter»	л	1,61	10 %	1,77	1 банка · банка 2,7 л	3 510 / банк	3 510		8
10	Краска интерьерная акриловая, матовая, класс истирания 1 — Tikkurila Harmony V503 «Winter»	л	3,54	10 %	3,89	2 банка · банка 2,7 л	3 510 / банк	7 020		8
Погонажные изделия и потолки										
11	Плинтус напольный МДФ под покраску, h=80 мм, крепление к стене — плинтус МДФ под покраску 80×16	м	70,34	10 %	77,37	33 шт · хлыст 2,4 м	368 / шт	12 144		1, 8
Двери										
12	Дверь входная Д-1, проём 900×2100 мм	шт	1		1	1 шт	по запросу			6
13	Дверь скрытого монтажа (короб под покраску) Д-2, проём 800×2100 мм	шт	2		2	2 шт	по запросу		≈ 30 дн.	6, 7
14	Дверь скрытого монтажа (короб под покраску) Д-3, проём 800×2100 мм	шт	1		1	1 шт	по запросу		≈ 30 дн.	6, 7
15	Дверь скрытого монтажа (короб под покраску) Д-4, проём 800×2100 мм	шт	1		1	1 шт	по запросу		≈ 30 дн.	6, 7
16	Дверь скрытого монтажа (короб под покраску) Д-5, проём 700×2100 мм	шт	1		1	1 шт	по запросу		≈ 30 дн.	6, 7
Черновые материалы — позиций 20, с ценой 2, итого 25 400 ₽										
Покрытия полов и облицовка										
17	Клей для паркетной и инженерной доски (эластичный, по ТУ изготовителя доски)	м²	65,78		65,78	фасовка по ТУ изделия	по запросу			2
Сухие смеси и гидроизоляция										
18	Клей плиточный цементный класса C2 TE S1 (ГОСТ Р 56387-2018) — Ceresit CM 17 или аналог	кг	278,81	10 %	306,69	13 мешок · мешок 25 кг	1 800 / меш.	23 400		8
19	Затирка цементная класса CG2WA, цвет — по колерной карте — Mapei Ultracolor Plus 132 или аналог	кг	3,47	10 %	3,82	2 упаковка · упак. 2 кг	1 000 / упак.	2 000		8
20	Гидроизоляция обмазочная полимерная, 2 слоя, лента в углах, манжеты на выводах	м²	18,15	10 %	19,96	фасовка по ТУ изделия	по запросу			2
21	Лента демпферная по периметру пола из плитки	м	20,36	10 %	22,40	23,00 м	по запросу			
22	Смесь цементно-песчаная для стяжки М200 (50 мм, 33 мм)	м³	3,89	5 %	4,08	фасовка по ТУ изделия	по запросу			2

Допущения и предложения на листе

Основа листа: размеры сняты со скана плана заказчика по размерным цепочкам, контрольный обмер на объекте не выполнялся (К-13); высота потолка 2700 мм принята: на плане заказчика не указана (К-11); толщины стен приняты: наружные 250 мм, перегородки 150 мм (на плане 85–190 мм) (К-13); разрешённая мощность 15 кВт принята по типовой квартире, технических условий нет (К-14); утолщение стены 190 × 1360 мм и элемент 1470 × 160 мм плана заказчика не определены (К-12); ниши санузла 2 закрыты перегородкой и фальш-стеной: проектное решение, на плане заказчика ниша у входа открыта (К-18); несущие стены не определены: до технического заключения все существующие стены считаются несущими (К-20); окна существующие и сохраняются; подоконная доска и глубина откосов не заданы — приняты, не замерены (К-27); подрайон климата не задан — принят не северный (жилые от 2,5 м) (К-29).

Знак «**» — предложение проектировщика, заказчиком не утверждено (согласовать с заказчиком): ИЗ-2, К-2, К-23: пол пом. 2, 7 — пирог пола: стяжка 33 мм и обмазочная гидроизоляция добавлены разработчиком проекта; артикул изделия не выбран: позиция описана характеристиками («аналог по характеристикам»), артикул выбирается при закупке; К-2, К-23: стены пом. 2, 7 — артикул изделия не выбран: позиция описана характеристиками («аналог по характеристикам»), артикул выбирается при закупке; К-23: пол пом. 1, 3–6, 8, плинтус пом. 1, 3–6, 8, фартук пом. 6 — артикул изделия не выбран: позиция описана характеристиками («аналог по характеристикам»), артикул выбирается при закупке.

См. лист открытых вопросов (лист 6, запись К-2; лист 7, записи К-11–К-14, К-18, К-20; лист 8, записи К-23, К-27, К-29; лист 9, запись ИЗ-2).

Изм.	Кол.уч	Лист	№ док.	Подп.	Дата
Разраб.		Кырлан А.С.			13.11.26
Пров.					
ГИП					
Н. контр.					
Утв.					

ГД-2026-003-АИ

Трёхкомнатная квартира

Общая площадь 78,95* м² · * размеры со скана, не замерены (реестр — л. 6–11, К-13)

Дизайн-проект интерьера трёхкомнатной квартиры

Стадия	Лист	Листов
РП	128	132

Смета материалов с ценами

М б/м

Кырлан Александр Сергеевич

Смета материалов с ценами (продолжение)

Все материалы с количеством, запасом, упаковкой, ценой и сроком · цены — ориентир по открытым прайсам, не оферта · работы не входят

Смета материалов с ценами (продолжение)

№	Позиция	Ед.	Нетто	Запас	С запасом	К закупке (упаковка)	Цена за ед., ₽	Сумма, ₽	Заказать заранее	Доп.
23	Смесь штукатурная гипсовая для машинного и ручного нанесения по маякам, слой до 10 мм	м²	198,37	10 %	218,21	фасовка по ТУ изделия	по запросу			2
Короба из ГКЛВ										
24	Лист ГКЛВ 12,5 мм, 2500 × 1200 мм, обшивка коробов в 2 слоя	м²	9,86	10 %	10,85	4 лист · лист 3,00 м²	по запросу			
25	Профиль стальной оцинкованный 27 × 28 мм: каркас коробов (стойки и направляющие)	м	24,23	10 %	26,65	9 шт · хлыст 3 м	по запросу			
Перегородки и облицовки из ГКЛВ										
26	Лист ГКЛВ 12,5 мм, 2500 × 1200 мм: обшивка перегородок и облицовок, 2 слоя на сторону	м²	14,56	10 %	16,02	6 лист · лист 3,00 м²	по запросу			
27	Профиль направляющий ПН 100: по потолку и полу, перемычки над проёмами	м	3,20	10 %	3,52	2 шт · хлыст 3 м	по запросу			
28	Профиль стоечный ПС 100: стойки через шаг каркаса и короткие над проёмами	м	9,30	10 %	10,23	4 шт · хлыст 3 м	по запросу			
29	Профиль усиленный УА 100 (2,0 мм): стойки по краям проёма на полную высоту	м	5,40	10 %	5,94	2 шт · хлыст 3 м	по запросу			
30	Плита минераловатная звукопоглощающая в полость каркаса, толщина по глубине профиля 100 мм	м²	2,85	10 %	3,14	фасовка по ТУ изделия	по запросу			2
31	Лента уплотнительная самоклеящаяся под профили по потолку, полу и у примыканий к стенам	м	7,90	10 %	8,69	9,00 м	по запросу			
32	Саморезы для ГКЛ по металлу (по слоям обшивки), дюбели для направляющих — по ТУ изготовителя системы	м²	14,56		14,56	фасовка по ТУ изделия	по запросу			2
33	Шпаклёвка для швов и мест креплений ГКЛВ под плитку (Q1)	м²	4,43	10 %	4,87	фасовка по ТУ изделия	по запросу			2
Лакокрасочные материалы										
34	Шпаклёвка финишная полимерная под окраску (стены и потолки, Q3)	м²	251,04	10 %	276,14	фасовка по ТУ изделия	по запросу			2
35	Грунтовка акриловая глубокого проникновения, 2 слоя	м²	284,60	10 %	313,06	фасовка по ТУ изделия	по запросу			2
Погонажные изделия и потолки										
36	Потолок подвесной ГКЛ/ГКЛВ по каркасу Knauf П113: листы, профили, подвесы, лента, шпаклёвка швов	м²	77,10		77,10	фасовка по ТУ изделия	по запросу			2
Электрика и слаботочные сети — позиций 40, с ценой 0, итого 0 ₽										
Слаботочные сети										
37	Кабель домофона — тип по системе поставщика	м	2,90		2,90	3,00 м	по запросу			3
38	Кабель коаксиальный RG-6 (75 Ом) к розеткам ТВ	м	30,30		30,30	31,00 м	по запросу			3
39	Кабель U/UTP кат. 6 (LAN, Wi-Fi и камеры по PoE)	м	62,30		62,30	63,00 м	по запросу			3
40	Гофротруба Ø20 для слаботочных линий, отдельно от силовых	м	86,00		86,00	86,00 м	по запросу			3
41	Розетка компьютерная RJ45, кат. 6, с рамкой и подрозетником	шт	3		3	3 шт	по запросу			
42	Розетка телевизионная (коаксиальная) с рамкой и подрозетником	шт	2		2	2 шт	по запросу			
43	Трубка или монитор домофона (поставка домофонной организации)	шт	1		1	1 шт	по запросу			
44	Щит слаботочный ЩС**: корпус, DIN-рейка, розетки 220 В	шт	1		1	1 шт	по запросу			
45	Патч-панель, портов не менее 5	шт	1		1	1 шт	по запросу			
Электрика: силовая часть										

Допущения и предложения на листе

Основа листа: размеры сняты со скана плана заказчика по размерным цепочкам, контрольный обмер на объекте не выполнялся (К-13); высота потолка 2700 мм принята: на плане заказчика не указана (К-11); толщины стен приняты: наружные 250 мм, перегородки 150 мм (на плане 85–190 мм) (К-13); разрешённая мощность 15 кВт принята по типовой квартире, технических условий нет (К-14); утолщение стены 190 × 1360 мм и элемент 1470 × 160 мм плана заказчика не определены (К-12); ниши санузла 2 закрыты перегородкой и фальш-стеной: проектное решение, на плане заказчика ниша у входа открыта (К-18); несущие стены не определены: до технического заключения все существующие стены считаются несущими (К-20); окна существующие и сохраняются; подоконная доска и глубина откосов не заданы — приняты, не замерены (К-27); подрайон климата не задан — принят не северный (жилые от 2,5 м) (К-29).

Знак «**» — предложение проектировщика, заказчиком не утверждено (согласовать с заказчиком): ИЗ-2, К-2, К-23: пол пом. 2, 7 — пирог пола: стяжка 33 мм и обмазочная гидроизоляция добавлены разработчиком проекта; артикул изделия не выбран: позиция описана характеристиками («аналог по характеристикам»), артикул выбирается при закупке; ИЗ-9, ИЗ-17, К-7: ЩС — щит слаботочный: место и состав; К-2, К-23: стены пом. 2, 7 — артикул изделия не выбран: позиция описана характеристиками («аналог по характеристикам»), артикул выбирается при закупке; К-23: пол пом. 1, 3–6, 8, плинтус пом. 1, 3–6, 8, фартук пом. 6 — артикул изделия не выбран: позиция описана характеристиками («аналог по характеристикам»), артикул выбирается при закупке.

См. лист открытых вопросов (лист 6, записи К-2, К-7; лист 7, записи К-11–К-14, К-18, К-20; лист 8, записи К-23, К-27, К-29; лист 9, записи ИЗ-2, ИЗ-9; лист 11, запись ИЗ-17).

Изм.	Кол.уч	Лист	№ док.	Подп.	Дата
Разраб.		Кырлан А.С.			13.11.26
Пров.					
ГИП					
Н. контр.					
Утв.					

ГД-2026-003-АИ

Трёхкомнатная квартира

Общая площадь 78,95* м² · * размеры со скана, не замерены (реестр — л. 6–11, К-13)

Дизайн-проект интерьера трёхкомнатной квартиры

Стадия	Лист	Листов
РП	129	132

Смета материалов с ценами (продолжение)

М б/м

Кырлан Александр Сергеевич

Смета материалов с ценами (продолжение)

Все материалы с количеством, запасом, упаковкой, ценой и сроком · цены — ориентир по открытым прайсам, не оферта · работы не входят

Смета материалов с ценами (продолжение)

№	Позиция	Ед.	Нетто	Запас	С запасом	К закупке (упаковка)	Цена за ед., ₽	Сумма, ₽	Заказать заранее	Доп.
46	Кабель силовой ВВГнг(А)-LS 3×1,5 мм²	м	247,20		247,20	248,00 м	по запросу			3
47	Кабель силовой ВВГнг(А)-LS 3×2,5 мм²	м	230,90		230,90	231,00 м	по запросу			3
48	Кабель силовой ВВГнг(А)-LS 3×6 мм²	м	15,40		15,40	16,00 м	по запросу			3
Электрика: щит										
49	Автоматический выключатель дифференциального тока (АВДТ) C10 A, 30 мА, тип A	шт	4		4	4 шт	по запросу			4
50	Автоматический выключатель дифференциального тока (АВДТ) C16 A, 30 мА, тип A	шт	9		9	9 шт	по запросу			4
51	Автоматический выключатель дифференциального тока (АВДТ) C32 A, 30 мА, тип A	шт	1		1	1 шт	по запросу			4
52	Корпус щита ЩРВ-П-48, IP41, 48 модулей	шт	1		1	1 шт	по запросу			4
53	Вводной автомат C63, 1P+N	шт	1		1	1 шт	по запросу			4
54	Вводное УЗО-А 63 А, 100 мА (селективное)	шт	1		1	1 шт	по запросу			4
55	УЗИП тип 2	шт	1		1	1 шт	по запросу			4
Электрика: механизмы и изделия										
56	Розетка с з/к и защитными шторками, 16 А	шт	36		36	36 шт	по запросу			4
57	Розетка IP44 с крышкой, 16 А	шт	3		3	3 шт	по запросу			4
58	Выключатель 1-клав.	шт	1		1	1 шт	по запросу			4
59	Выключатель 1-клав. перекрёстный	шт	3		3	3 шт	по запросу			4
60	Выключатель 2-клав.	шт	2		2	2 шт	по запросу			4
61	Выключатель 2-клав. (перекрёстная + проходная)	шт	2		2	2 шт	по запросу			4
62	Выключатель 2-клав. (проходная + обычная)	шт	4		4	4 шт	по запросу			4
63	Выключатель 2-клав. проходной	шт	2		2	2 шт	по запросу			4
64	Светорегулятор 1-канальный, задний фронт (LED)	шт	4		4	4 шт	по запросу			4
65	Датчик движения ночной подсветки	шт	1		1	1 шт	по запросу			4
66	Рамка 1-постовая	шт	47		47	47 шт	по запросу			4
67	Рамка 2-постовая	шт	5		5	5 шт	по запросу			4
68	Коробка установочная (подрозетник) Ø68	шт	57		57	57 шт	по запросу			4
69	Вывод кабеля под прибор (клеммник)	шт	7		7	7 шт	по запросу			4
70	Коробка уравнивания потенциалов КУП	шт	2		2	2 шт	по запросу			4
71	Блок питания LED 24 В, 200 Вт, дим.	шт	2		2	2 шт	по запросу			4
72	Блок питания LED 24 В, 20 Вт	шт	1		1	1 шт	по запросу			4
73	Блок питания LED 24 В, 300 Вт, дим.	шт	1		1	1 шт	по запросу			4

Допущения и предложения на листе

Основа листа: размеры сняты со скана плана заказчика по размерным цепочкам, контрольный обмер на объекте не выполнялся (К-13); высота потолка 2700 мм принята: на плане заказчика не указана (К-11); толщины стен приняты: наружные 250 мм, перегородки 150 мм (на плане 85–190 мм) (К-13); разрешённая мощность 15 кВт принята по типовой квартире, технических условий нет (К-14); утолщение стены 190 × 1360 мм и элемент 1470 × 160 мм плана заказчика не определены (К-12); ниши санузла 2 закрыты перегородкой и фальш-стеной: проектное решение, на плане заказчика ниша у входа открыта (К-18); несущие стены не определены: до технического заключения все существующие стены считаются несущими (К-20); окна существующие и сохраняются; подоконная доска и глубина откосов не заданы — приняты, не замерены (К-27); подрайон климата не задан — принят не северный (жилые от 2,5 м) (К-29).

Знак «**» — предложение проектировщика, заказчиком не утверждено (согласовать с заказчиком): ИЗ-2, К-2, К-23: пол пом. 2, 7 — пирог пола: стяжка 33 мм и обмазочная гидроизоляция добавлены разработчиком проекта; артикул изделия не выбран: позиция описана характеристиками («аналог по характеристикам»), артикул выбирается при закупке; К-2, К-23: стены пом. 2, 7 — артикул изделия не выбран: позиция описана характеристиками («аналог по характеристикам»), артикул выбирается при закупке; К-23: пол пом. 1, 3–6, 8, плинтус пом. 1, 3–6, 8, фартук пом. 6 — артикул изделия не выбран: позиция описана характеристиками («аналог по характеристикам»), артикул выбирается при закупке.

См. лист открытых вопросов (лист 6, запись К-2; лист 7, записи К-11–К-14, К-18, К-20; лист 8, записи К-23, К-27, К-29; лист 9, запись ИЗ-2).

Изм.	Кол.уч	Лист	№ док.	Подп.	Дата
Разраб.		Кырлан А.С.			13.11.26
Пров.					
ГИП					
Н. контр.					
Утв.					

ГД-2026-003-АИ

Трёхкомнатная квартира

Общая площадь 78,95* м² · * размеры со скана, не замерены (реестр — л. 6–11, К-13)

Дизайн-проект интерьера трёхкомнатной квартиры

Стадия	Лист	Листов
РП	130	132

Смета материалов с ценами (продолжение)

М б/м

Кырлан Александр Сергеевич

Смета материалов с ценами (продолжение)

Все материалы с количеством, запасом, упаковкой, ценой и сроком · цены — ориентир по открытым прайсам, не оферта · работы не входят

Смета материалов с ценами (продолжение)

№	Позиция	Ед.	Нетто	Запас	С запасом	К закупке (упаковка)	Цена за ед., ₽	Сумма, ₽	Заказать заранее	Доп.
74	Блок питания LED 24 В, 60 Вт, дим.	шт	1		1	1 шт	по запросу			4
75	Извещатель дымовой автономный	шт	3		3	3 шт	по запросу			4
76	Извещатель тепловой	шт	3		3	3 шт	по запросу			4
Сантехника — позиций 38, с ценой 0, итого 0 ₽										
Сантехника: санитарные приборы										
77	Ванна встраиваемая акриловая 1600×750 мм, с каркасом, экраном и отверстием слив-перелив — акриловая 1600×750, смеситель настенный	шт	1		1	1 шт	по запросу			5
78	Унитаз подвесной безободковый, с сиденьем микролифт, крепёж и звукоизолирующая прокладка	шт	2		2	2 шт	по запросу			5, 1
79	Инсталляция для подвесного унитаза: рама высотой 1120 мм, бачок, клавиша смыва (ось клавиши 1050 мм от чистого пола)	шт	2		2	2 шт	по запросу			5, 1
80	Умывальник подвесной 450×600 мм, с отверстием под смеситель и переливом	шт	1		1	1 шт	по запросу			5, 1
81	Умывальник подвесной 350×500 мм, с отверстием под смеситель и переливом	шт	1		1	1 шт	по запросу			5, 1
82	Поддон душевой низкий 800×800 мм, с сифоном и выпуском Ø50, на ножках/подиуме	шт	1		1	1 шт	по запросу			5, 1
83	Мойка кухонная врезная 700×480 мм, с переливом	шт	1		1	1 шт	по запросу			5, 1
84	Полотенцесушитель электрический, IP44, с терморегулятором	шт	2		2	2 шт	по запросу			5, 1
Сантехника: смесители, сифоны и арматура приборов										
85	Смеситель для ванны настенный однорычажный, межосевое 150 мм, с душевым набором (лейка, шланг, держатель)	шт	1		1	1 шт	по запросу			5, 1
86	Смеситель для умывальника однорычажный, с донным клапаном	шт	2		2	2 шт	по запросу			5, 1
87	Душевая система скрытого монтажа с термостатом: встраиваемая часть, верхний душ, ручная лейка	шт	1		1	1 шт	по запросу			5, 1
88	Смеситель кухонный однорычажный, высокий излив	шт	1		1	1 шт	по запросу			5, 1
89	Обвязка ванны слив-перелив Ø40/50 с сифоном	шт	1		1	1 шт	по запросу			5, 1
90	Сифон для умывальника бутылочный Ø32/40–50, с гофрой к выпуску	шт	2		2	2 шт	по запросу			5, 1
91	Сифон для мойки Ø40/50	шт	1		1	1 шт	по запросу			5, 1
92	Сифон для посудомоечной машины с обратным клапаном, на выводе слива Ø40	шт	1		1	1 шт	по запросу			5, 1
93	Сифон для стиральной машины встраиваемый в стену Ø50, с обратным клапаном	шт	1		1	1 шт	по запросу			5, 1
94	Кран угловой ½"×½" с гибкой подводкой 40 см (умывальники, мойка)	шт	6		6	6 шт	по запросу			5, 1
95	Кран шаровой угловой ½"×¾" для подключения стиральной и посудомоечной машины	шт	2		2	2 шт	по запросу			5, 1
Сантехника: трубопроводы										
96	Труба полипропиленовая PP-R PN20 Ø20×3,4 (В1) — ГОСТ 32415-2013	м	18,50	10 %	18,50	18,50 м	по запросу			5
97	Труба PP-R, армированная стекловолокном, PN20 Ø20×2,8 (Т3) — ГОСТ 32415-2013	м	13,50	10 %	13,50	13,50 м	по запросу			5
98	Труба канализационная ПП Ø40 (К1) — ГОСТ 32414-2013	м	1,00	10 %	1,00	1,00 м	по запросу			5
99	Труба канализационная ПП Ø50 (К1) — ГОСТ 32414-2013	м	11,00	10 %	11,00	11,00 м	по запросу			5

Допущения и предложения на листе

Основа листа: размеры сняты со скана плана заказчика по размерным цепочкам, контрольный обмер на объекте не выполнялся (К-13); высота потолка 2700 мм принята: на плане заказчика не указана (К-11); толщины стен приняты: наружные 250 мм, перегородки 150 мм (на плане 85–190 мм) (К-13); разрешённая мощность 15 кВт принята по типовой квартире, технических условий нет (К-14); утолщение стены 190 × 1360 мм и элемент 1470 × 160 мм плана заказчика не определены (К-12); ниши санузла 2 закрыты перегородкой и фальш-стеной: проектное решение, на плане заказчика ниша у входа открыта (К-18); несущие стены не определены: до технического заключения все существующие стены считаются несущими (К-20); окна существующие и сохраняются; подоконная доска и глубина откосов не заданы — приняты, не замерены (К-27); подрайон климата не задан — принят не северный (жилые от 2,5 м) (К-29).

Знак «**» — предложение проектировщика, заказчиком не утверждено (согласовать с заказчиком): ИЗ-2, К-2, К-23: пол пом. 2, 7 — пирог пола: стяжка 33 мм и обмазочная гидроизоляция добавлены разработчиком проекта; артикул изделия не выбран: позиция описана характеристиками («аналог по характеристикам»), артикул выбирается при закупке; К-2, К-23: стены пом. 2, 7 — артикул изделия не выбран: позиция описана характеристиками («аналог по характеристикам»), артикул выбирается при закупке; К-23: пол пом. 1, 3–6, 8, плинтус пом. 1, 3–6, 8, фартук пом. 6 — артикул изделия не выбран: позиция описана характеристиками («аналог по характеристикам»), артикул выбирается при закупке.

См. лист открытых вопросов (лист 6, запись К-2; лист 7, записи К-11–К-14, К-18, К-20; лист 8, записи К-23, К-27, К-29; лист 9, запись ИЗ-2).

Изм.	Кол.уч	Лист	№ док.	Подп.	Дата
Разраб.		Кырлан А.С.			13.11.26
Пров.					
ГИП					
Н. контр.					
Утв.					

ГД-2026-003-АИ

Трёхкомнатная квартира

Общая площадь 78,95* м² · * размеры со скана, не замерены (реестр — л. 6–11, К-13)

Дизайн-проект интерьера трёхкомнатной квартиры

Стадия	Лист	Листов
РП	131	132

Смета материалов с ценами (продолжение)

М б/м

Кырлан Александр Сергеевич

Смета материалов с ценами (окончание)

ПРЕДВАРИТЕЛЬНО · не для производства работ · открыто пунктов: 28 (реестр — л. 6–11)

Все материалы с количеством, запасом, упаковкой, ценой и сроком · цены — ориентир по открытым прайсам, не оферта · работы не входят

Смета материалов с ценами (продолжение)

№	Позиция	Ед.	Нетто	Запас	С запасом	К закупке (упаковка)	Цена за ед., ₽	Сумма, ₽	Заказать заранее	Доп.
100	Труба канализационная ПП Ø110 (К1) — ГОСТ 32414-2013	м	4,00	10 %	4,00	4,00 м	по запросу			5
Сантехника: фасонные части и выводы										
101	Отвод канализационный ПП 45° Ø40 — ГОСТ 32414-2013	шт	2		2	2 шт	по запросу			5
102	Отвод канализационный ПП 45° Ø50 — ГОСТ 32414-2013	шт	20		20	20 шт	по запросу			5
103	Отвод канализационный ПП 45° Ø110 — ГОСТ 32414-2013	шт	10		10	10 шт	по запросу			5
104	Тройник канализационный ПП 45° (врезки ветвей) — ГОСТ 32414-2013	шт	8		8	8 шт	по запросу			5
105	Ревизия канализационная ПП (после поворота трассы) — ГОСТ 32414-2013	шт	9		9	9 шт	по запросу			5
106	Фитинги PP-R Ø20: тройники, угольники 90° (ветви и повороты В1, Т3) — ГОСТ 32415-2013	шт	34		34	34 шт	по запросу			5
107	Водорозетка PP-R Ø20×½" настенная, с креплением — ГОСТ 32415-2013	шт	14		14	14 шт	по запросу			5
Сантехника: узлы ввода, люки, короба										
108	Кран шаровой латунный Ду15 PN16 (отключение ввода)	шт	4		4	4 шт	по запросу			5, 1
109	Фильтр сетчатый косой Ду15	шт	4		4	4 шт	по запросу			5, 1
110	Счётчик воды крыльчатый Ду15 (ХВ, ГВ), с поверкой	шт	4		4	4 шт	по запросу			5, 1
111	Клапан обратный Ду15	шт	4		4	4 шт	по запросу			5, 1
112	Люк ревизионный нажимной под плитку 300×400 мм	шт	2		2	2 шт	по запросу			5, 1
113	Звукоизоляция стояка К1 в коробе: рулонный звукоизоляционный материал ≥ 10 мм, обмотка стояка на высоту этажа	м	5,40		5,40	5,40 м	по запросу			5, 1
114	Короб К1 над полом: профиль ПН/ПС, ГКЛВ 12,5 мм под плитку	м	2,40		2,40	2,40 м	по запросу			5, 1
	ИТОГО материалы (позиций с ценой 13 из 114; без цены 101 — «по запросу», в итог не входят)							**762 725**		

Примечания

1. Количества — из единой книги материалов проекта: тот же расход, что в спецификации отделочных материалов, смете и списке покупок. Запас — на подрезку и бой; норма запаса печатается в графе «Запас», её основание — в отдельном документе «Смета на материалы».
2. Цены — нижняя граница открытых прайсов (прайсы собраны 21.09.2026, часть расценок сверена повторно 06.10.2026 и 08.11.2026, Москва); не предложение (оферта) магазинов. Цены нет — «по запросу», позиция в итог не входит. Работы в эту смету не входят (они — на листе «Смета проекта»).
3. Доп. 1. Изделие не выбрано: позиция описана по характеристикам («аналог»); марка, артикул и цена определяются при выборе изделия.
4. Доп. 2. Фасовка не задана в данных: количество дано в мерах расчёта, число упаковок определяется по выбранному продукту (расход и тара — по ТУ).
5. Доп. 3. Длина кабеля — по длинам групп щита из данных электрика; запас на подрезку в длину не заложен — берите бухту с запасом 5–10 %.
6. Доп. 4. Механизмы, рамки и подрозетники — по ведомости изделий электрика; серию механизмов выбирает заказчик.
7. Доп. 5. Трубы и фасонные части — по трассам листа разводки, +10 % на подрезку (уже в количестве); модели приборов заказчик выбирает сам.
8. Доп. 6. Двери: цена и срок называет поставщик после выбора изделия; в смету стоят только если цена задана в данных.
9. Доп. 7. Срок поставки — из данных проекта; если срок не задан, указан типовой диапазон практики как ориентир, а не срок поставщика.
10. Доп. 8. Цена — нижняя граница открытых прайс-листов на дату сбора (книга цен проекта); не коммерческое предложение магазина.
11. Доп. 9. Доли по помещениям справочные: общая закупка делится пропорционально площади (длине, числу), по которой считается позиция.

Допущения и предложения на листе

Основа листа: размеры сняты со скана плана заказчика по размерным цепочкам, контрольный обмер на объекте не выполнялся (К-13); высота потолка 2700 мм принята: на плане заказчика не указана (К-11); толщины стен приняты: наружные 250 мм, перегородки 150 мм (на плане 85–190 мм) (К-13); разрешённая мощность 15 кВт принята по типовой квартире, технических условий нет (К-14); утолщение стены 190 × 1360 мм и элемент 1470 × 160 мм плана заказчика не определены (К-12); ниши санузла 2 закрыты перегородкой и фальш-стеной: проектное решение, на плане заказчика ниша у входа открыта (К-18); несущие стены не определены: до технического заключения все существующие стены считаются несущими (К-20); окна существующие и сохраняются; подоконная доска и глубина откосов не заданы — приняты, не замерены (К-27); подрайон климата не задан — принят не северный (жилые от 2,5 м) (К-29).

Знак «**» — предложение проектировщика, заказчиком не утверждено (согласовать с заказчиком): ИЗ-2, К-2, К-23: пол пом. 2, 7 — пирог пола: стяжка 33 мм и обмазочная гидроизоляция добавлены разработчиком проекта; артикул изделия не выбран: позиция описана характеристиками («аналог по характеристикам»), артикул выбирается при закупке; К-2, К-23: стены пом. 2, 7 — артикул изделия не выбран: позиция описана характеристиками («аналог по характеристикам»), артикул выбирается при закупке; К-23: пол пом. 1, 3–6, 8, плинтус пом. 1, 3–6, 8, фартук пом. 6 — артикул изделия не выбран: позиция описана характеристиками («аналог по характеристикам»), артикул выбирается при закупке.

См. лист открытых вопросов (лист 6, запись К-2; лист 7, записи К-11–К-14, К-18, К-20; лист 8, записи К-23, К-27, К-29; лист 9, запись ИЗ-2).

Изм.	Кол.уч	Лист	№ док.	Подп.	Дата
Разраб.		Кырлан А.С.			13.11.26
Пров.					
ГИП					
Н. контр.					
Утв.					

ГД-2026-003-АИ

Трёхкомнатная квартира

Общая площадь 78,95* м² · * размеры со скана, не замерены (реестр — л. 6–11, К-13)

Дизайн-проект интерьера трёхкомнатной квартиры

Стадия	Лист	Листов
РП	132	132

Смета материалов с ценами (окончание)

М б/м

Кырлан Александр Сергеевич

выпуск 13.11.2026 № 6f3a8abb2c · стр. 142 из 157

11

Визуализации

Кырлан Александр Сергеевич

выпуск 13.11.2026 · 6f3a8abb2c · стр. 143 из 157



Планировочное решение · вид сверху

выпуск 13.11.2026 № 6f3a8abb2c · стр. 144 из 157



Кухня-гостиная · потолок

Трёхкомнатная квартира · визуализация 2 из 14

выпуск 13.11.2026 № 6f3a8abb2c · стр. 145 из 157



Спальня 1 · потолок

выпуск 13.11.2026 № 6f3a8abb2c · стр. 146 из 157



Ванная · стена Б

Трёхкомнатная квартира · визуализация 4 из 14

выпуск 13.11.2026 № 6f3a8abb2c · стр. 147 из 157



Ванная · стена Г

выпуск 13.11.2026 № 6f3a8abb2c · стр. 148 из 157



Санузел 2 · стена Б

выпуск 13.11.2026 № 6f3a8abb2c · стр. 149 из 157


выпуск 13.11.2026 № 6f3a8abb2c · стр. 150 из 157

Спальня 1 · стена А



Спальня 1 · стена Б

выпуск 13.11.2026 № 6f3a8abb2c · стр. 151 из 157

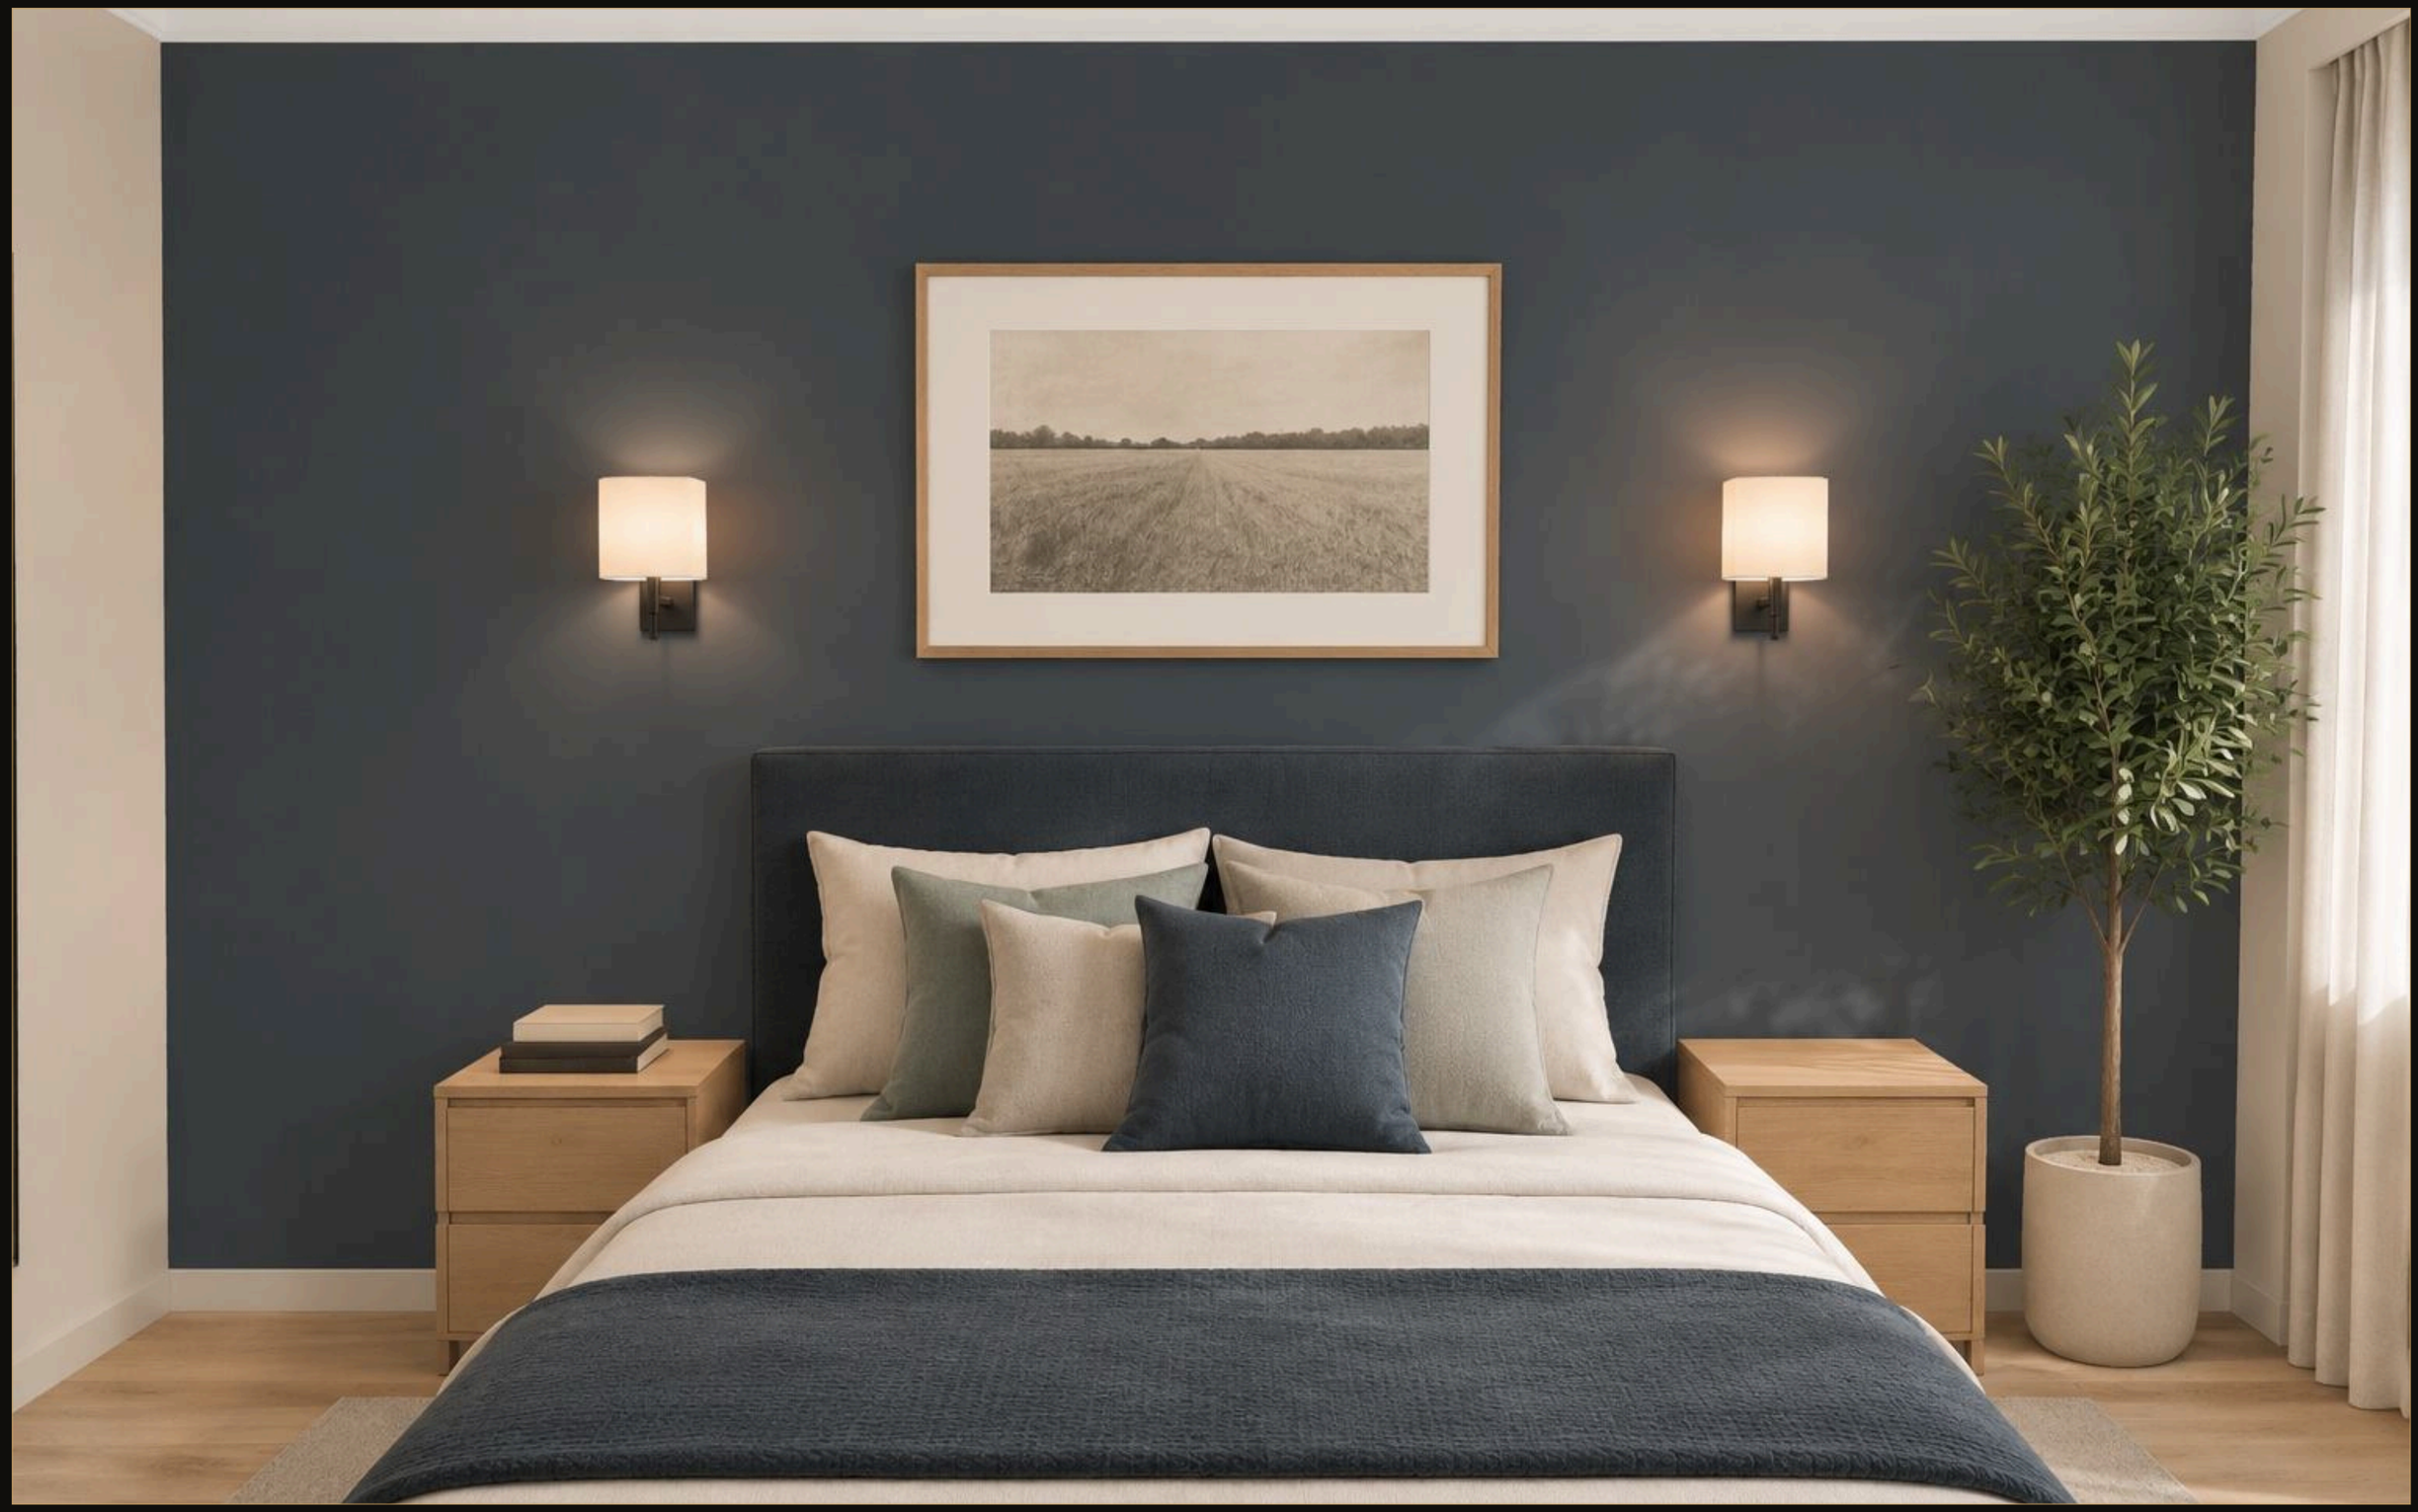

Спальня 2 · стена А

Трёхкомнатная квартира · визуализация 9 из 14

выпуск 13.11.2026 № 6f3a8abb2c · стр. 152 из 157

выпуск 13.11.2026 № 6f3a8abb2c · стр. 153 из 157



Спальня 2 · стена Г



Коридор · стена А

выпуск 13.11.2026 № 6f3a8abb2c · стр. 154 из 157



Кухня-гостиная · стена B

Трёхкомнатная квартира · визуализация 12 из 14

выпуск 13.11.2026 № 6f3a8abb2c · стр. 155 из 157



Кухня-гостиная · стена Г

выпуск 13.11.2026 № 6f3a8abb2c · стр. 156 из 157



Гардеробная · общий вид

Трёхкомнатная квартира · визуализация 14 из 14

выпуск 13.11.2026 № 6f3a8abb2c · стр. 157 из 157