
LINEA

ДИЗАЙН-ПРОЕКТ ИНТЕРЬЕРА

Квартира 56 м²

ЖК «Северный парк», Москва · джапанди

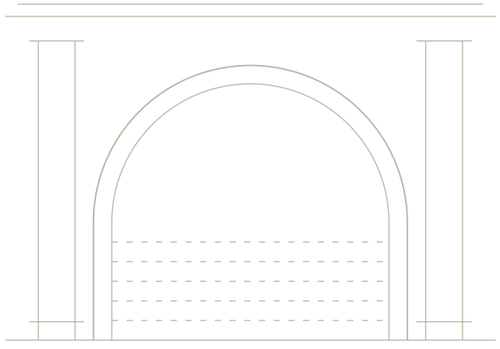

ПАЛИТРА ОТДЕЛКИ

NCS S 0804-Y30	F485	F&B No. 298	X447	NCS S 5010-G70
53 %	33 %	6 %	4 %	4 %

АВТОР ПРОЕКТА

Кырлан Александр Сергеевич

Ноябрь 2026



Визуализация гостиной · 3D

ОБЩАЯ ПЛОЩАДЬ	ПОМЕЩЕНИЙ	СТАДИЯ	ШИФР	ОСНОВА
56,37 м²	5, из них жилых 3	Рабочий проект · предварительно	ГД-2026-011-АИ	план заказчика, без обмера

Изм.	Кол.уч	Лист	№ док.	Подп.	Дата	ГД-2026-011-АИ		
						Квартира 56 м² ЖК «Северный парк», Москва		
Разраб.		Кырлан А.С.			13.11.26	Дизайн-проект интерьера	Стадия: РП	Лист: 1 / Листов: 119
Пров.								
ГИП								
Н. контр.						Титульный лист	Кырлан Александр Сергеевич	
Утв.						М б/м		

выпуск 13.11.2026 № eb7810814f · стр. 1 из 139

Общие данные

Комплект ГД-2026-011-АИ · Квартира 56 м² · джапанди

ПРЕДВАРИТЕЛЬНО · не для производства работ · открыто пунктов: 13 (реестр — л. 6, 7)

Допущения и предложения на листе. См. лист открытых вопросов (листы 6, 7).

Ведомость рабочих чертежей основного комплекта ГД-2026-011-АИ

Лист	Наименование	Примечание
1	Титульный лист	
2	Общие данные	
3	Общие данные	
4	Общие данные	
5	Общие данные	
6	Открытые вопросы, принятые допущения и конфликты. Лист 1 из 2	
7	Открытые вопросы, принятые допущения и конфликты. Лист 2 из 2	
8	Задание на контрольный обмер и обследование. Лист 1 из 4	
9	Задание на контрольный обмер и обследование. Лист 2 из 4	
10	Задание на контрольный обмер и обследование. Лист 3 из 4	
11	Задание на контрольный обмер и обследование. Лист 4 из 4	
12	График закупок и работ. Лист 1 из 3	
13	График закупок и работ. Лист 2 из 3	
14	График закупок и работ. Лист 3 из 3	
15	Календарный график работ и закупок	
16	Чек-лист приёмки по этапам. Лист 1 из 4	
17	Чек-лист приёмки по этапам. Лист 2 из 4	
18	Чек-лист приёмки по этапам. Лист 3 из 4	
19	Чек-лист приёмки по этапам. Лист 4 из 4	
20	Лист → мастер	
21	Обмерный план	
22	План демонтажа и монтажа перегородок	
23	План демонтажа	
24	План монтажа перегородок	
25	План дверей и ведомость заполнения проёмов	
26	Концепция интерьера	
27	План расстановки мебели	
28	Спецификация мебели и оборудования	
29	Спецификация мебели и оборудования (продолжение)	
30	Спецификация мебели и оборудования (продолжение)	

Ведомость рабочих чертежей основного комплекта ГД-2026-011-АИ (продолжение)

Лист	Наименование	Примечание
31	Спецификация мебели и оборудования (продолжение)	
32	План розеток и электровыводов	
33	План освещения	
34	План выключателей и схема включения	
35	Ведомость электроточек и изделий	
36	Ведомость электроточек и изделий (продолжение)	
37	Однолинейная схема щита	
38	План принципиальных трасс	
39	Таблица нагрузок щита	
40	План слаботочных сетей	
41	План вентиляции	
42	План отопления	
43	План выводов сантехники	
44	Схема разводки водопровода и канализации	
45	Аксонометрическая схема В1 (холодное водоснабжение)	
46	Аксонометрическая схема Т3 (горячее водоснабжение)	
47	Аксонометрическая схема К1 (канализация)	
48	Развёртки мокрых зон: выводы ВК. Гостиная-кухня	
49	Развёртки мокрых зон: выводы ВК. Санузел	
50	Спецификация сантехнического оборудования	
51	Техническое задание на подбор светильников	
52	Схема каркаса перегородки П-2	
53	План потолков	

Общие указания — лист 5: ±0,000 — чистый пол; несущие конструкции и сети дома — по отдельному проекту; скрытые работы — по актам. Открытые вопросы и допущения — листы 6, 7.

Изм.	Кол.уч	Лист	№ док.	Подп.	Дата
Разраб.		Кырлан А.С.			13.11.26
Пров.					
ГИП					
Н. контр.					
Утв.					

ГД-2026-011-АИ

Квартира 56 м²

ЖК «Северный парк», Москва

Дизайн-проект интерьера

Стадия	Лист	Листов
РП	2	119

Общие данные

М б/м

Кырлан Александр Сергеевич

выпуск 13.11.2026 № eb78108814f · стр. 2 из 139

Общие данные

Комплект ГД-2026-011-АИ · лист 2 общих данных (продолжение)

Допущения и предложения на листе. См. лист открытых вопросов (листы 6, 7).

Ведомость рабочих чертежей основного комплекта ГД-2026-011-АИ (продолжение)

Лист	Наименование	Примечание
54	Разрезы и узлы потолков	
55	Разрезы и узлы потолков (продолжение)	
56	Сечения потолков М 1:10	
57	Раскладка плитки. Планы полов	
58	Раскладка плитки. Прихожая. Фартук кухни	
59	Раскладка плитки. Санузел. Развёртки стен	
60	План полов	
61	Ведомость отделки помещений	
62	Колерная карта	
63	Спецификация отделочных материалов	
64	Концепция декора и визуализации	
65	План текстиля и декора	
66	Шторы и карнизы	
67	Ведомость текстиля	
68	Ведомость декора. Схемы развески	
69	Схемы развески (продолжение)	
70	Встроенная мебель. Схема расположения	
71	Шкаф распашной Сп4	
72	Шкаф распашной Дт2	
73	Шкаф-купе Пр1	
74	Система хранения Пр3	
75	Кухня (пом. 1). Развёртка гарнитура	
76	Кухня (пом. 1). Развёртка гарнитура: вид без фасадов и разрезы	
77	Кухня (пом. 1). Монтажная схема	
78	Кухня (пом. 1). Столешница: план	
79	Шкафы. Монтажная схема	
80	Ведомости изделий, техники и фурнитуры	
81	Сводка листовых материалов и кромки	
82	Реестр марок отделки и позиций альбома	
83	Схема расположения развёрток и узлов	

Ведомость рабочих чертежей основного комплекта ГД-2026-011-АИ (продолжение)

Лист	Наименование	Примечание
84	Развёртка стены Г. Гостиная-кухня (пом. 1), кухонный фронт	
85	Развёртка стены А. Гостиная-кухня (пом. 1)	
86	Развёртка стены Б. Гостиная-кухня (пом. 1)	
87	Развёртка стены В. Гостиная-кухня (пом. 1)	
88	Развёртка стены А. Спальня (пом. 2)	
89	Развёртка стены Б. Спальня (пом. 2)	
90	Развёртка стены В. Спальня (пом. 2)	
91	Развёртка стены Г. Спальня (пом. 2)	
92	Развёртка стены А. Детская (пом. 3)	
93	Развёртки стен Б, Г. Детская (пом. 3)	
94	Развёртка стены В. Детская (пом. 3)	
95	Развёртка стены А. Санузел (пом. 4)	
96	Развёртка стены Б. Санузел (пом. 4)	
97	Развёртки стен В, Г. Санузел (пом. 4)	
98	Развёртка стены А. Прихожая (пом. 5)	
99	Развёртка стены Б. Прихожая (пом. 5)	
100	Развёртка стены В. Прихожая (пом. 5)	
101	Развёртка стены Г. Прихожая (пом. 5)	
102	Узлы. Лист 1 из 2	
103	Узлы. Лист 2 из 2	
104	Ведомость объёмов работ	
105	Ведомость объёмов работ (продолжение)	
106	Ведомость объёмов работ (окончание)	

Общие указания — лист 5: ±0,000 — чистый пол; несущие конструкции и сети дома — по отдельному проекту; скрытые работы — по актам. Открытые вопросы и допущения — листы 6, 7.

Изм.	Кол.уч	Лист	№ док.	Подп.	Дата	ГД-2026-011-АИ		
						Квартира 56 м² ЖК «Северный парк», Москва		
Разраб.		Кырлан А.С.			13.11.26	Дизайн-проект интерьера	Стадия: РП	Лист: 3 / Листов: 119
Пров.								
ГИП						Общие данные М б/м	Кырлан Александр Сергеевич	
Н. контр.								
Утв.								

выпуск 13.11.2026 № eb78108814f · стр. 3 из 139

Общие данные

Комплект ГД-2026-011-АИ · лист 3 общих данных (продолжение)

Ведомость рабочих чертежей основного комплекта ГД-2026-011-АИ (продолжение)

Лист	Наименование	Примечание
107	Спецификация материалов	
108	Спецификация материалов (продолжение)	
109	Спецификация материалов (окончание)	
110	Смета ориентировочная	
111	Смета ориентировочная (окончание)	
112	Смета проекта: этапы, помещения, итог	
113	Смета проекта: этапы, помещения, итог (продолжение)	
114	Смета проекта: этапы, помещения, итог (окончание)	
115	Смета материалов с ценами	
116	Смета материалов с ценами (продолжение)	
117	Смета материалов с ценами (продолжение)	
118	Смета материалов с ценами (продолжение)	
119	Смета материалов с ценами (окончание)	

Ведомость ссылочных и прилагаемых документов

Обозначение	Наименование	Примечание
	Ссылочные документы	
ГОСТ 21.201-2011	СПДС. Условные графические изображения элементов зданий, сооружений и конструкций	
ГОСТ 21.205-2016	СПДС. Условные обозначения элементов санитарно-технических систем	
ГОСТ 21.210-2014	СПДС. Изображения условные графические электрооборудования и проводок на планах	
ГОСТ 2.306-68	ЕСКД. Обозначения графические материалов и правила их нанесения на чертежах	
	Прилагаемые документы	
ГД-2026-011-АИ.В1	Визуализация. Вид сверху (3D): планировка с мебелью, текстилем и декором	альбом визуализаций
ГД-2026-011-АИ.В2	Визуализация. Потолок: Спальня (пом. 2)	
ГД-2026-011-АИ.В3	Визуализация. Потолок: Прихожая (пом. 5)	
ГД-2026-011-АИ.В4	Визуализация. Потолок: Детская (пом. 3)	
ГД-2026-011-АИ.В5	Визуализация. Потолок: Гостиная-кухня (пом. 1)	
ГД-2026-011-АИ.В6	Визуализация. Интерьер: Санузел (пом. 4), стена А	
ГД-2026-011-АИ.В7	Визуализация. Интерьер: Санузел (пом. 4), стена Г	
ГД-2026-011-АИ.В8	Визуализация. Интерьер: Спальня (пом. 2), стена А	
ГД-2026-011-АИ.В9	Визуализация. Интерьер: Спальня (пом. 2), стена В	
ГД-2026-011-АИ.В10	Визуализация. Интерьер: Спальня (пом. 2), стена Г	
ГД-2026-011-АИ.В11	Визуализация. Интерьер: Прихожая (пом. 5), общий вид	
ГД-2026-011-АИ.В12	Визуализация. Интерьер: Детская (пом. 3), стена А	
ГД-2026-011-АИ.В13	Визуализация. Интерьер: Детская (пом. 3), стена Б	
ГД-2026-011-АИ.В14	Визуализация. Интерьер: Детская (пом. 3), стена Г	
ГД-2026-011-АИ.В15	Визуализация. Интерьер: Гостиная-кухня (пом. 1), стена А	
ГД-2026-011-АИ.В16	Визуализация. Интерьер: Гостиная-кухня (пом. 1), стена Б	

Допущения и предложения на листе

Основа листа: размеры помещений и положение проёмов введены заказчиком в брифе, на объекте не замерены (К-1); высота потолка 2700 мм — по брифу заказчика, не замерена (К-2); толщины стен приняты по брифу: наружные 200 мм, внутренние 150 мм — не обмерены (К-1); тип дома монолитный, перекрытие 200 мм — по брифу заказчика, документов нет (К-3); планировка (стены, проёмы, объединение кухни и гостиной, расширение санузла) — по брифу без обмера и плана БТИ (К-7); разрешённая мощность 10 кВт принята, ТУ не переданы (К-8); вентканалы приняты, в брифе не заданы (К-9); подрайон климата не задан — принят не северный (жилые от 2,5 м) (К-10).

См. лист открытых вопросов (лист 6, записи К-1–К-3, К-7–К-10).

Общие указания — лист 5: ±0,000 — чистый пол; несущие конструкции и сети дома — по отдельному проекту; скрытые работы — по актам. Открытые вопросы и допущения — листы 6, 7.

Изм.	Кол.уч	Лист	№ док.	Подп.	Дата
Разраб.		Кырлан А.С.			13.11.26
Пров.					
ГИП					
Н. контр.					
Утв.					

ГД-2026-011-АИ

Квартира 56 м²

ЖК «Северный парк», Москва

Дизайн-проект интерьера

Стадия	Лист	Листов
РП	4	119

Общие данные

М б/м

Кырлан Александр Сергеевич

выпуск 13.11.2026 № eb7810814f · стр. 4 из 139

Общие данные

Комплект ГД-2026-011-АИ · лист 4 общих данных (продолжение)

Ведомость ссылочных и прилагаемых документов (продолжение)

Обозначение	Наименование	Примечание
ГД-2026-011-АИ.В17	Визуализация. Интерьер: Гостиная-кухня (пом. 1), стена В	
ГД-2026-011-АИ.В18	Визуализация. Интерьер: Гостиная-кухня (пом. 1), стена Г	

Состав дизайн-проекта

Раздел	Состав	Листы
Обложка	Дизайн-проект интерьера; Квартира 56 м²; автор проекта — Кырлан Александр Сергеевич	1 с.
Концепция	Стиль Джапанди: концепция интерьера, палитра и материалы (колерная карта — лист 62)	л. 26
Визуализации	18 изобр.: Вид сверху (3D): планировка с мебелью, текстилем и декором; Потолок: Спальня; Потолок: Прихожая; Потолок: Детская; Потолок: Гостиная-кухня; Санузел, стена А; Санузел, стена Г; Спальня, стена А; Спальня, стена В; Спальня, стена Г; Прихожая, общий вид; Детская, стена А; Детская, стена Б; Детская, стена Г; Гостиная-кухня, стена А; Гостиная-кухня, стена Б; Гостиная-кухня, стена В; Гостиная-кухня, стена Г	В1–В18
Рабочие чертежи	планы, развёртки, узлы (развёртки и узлы — листы 48, 49, 83, 93, 97, 102, 103)	л. 1–119
Спецификации и ведомости	оборудование, изделия, отделка, электроточки	л. 25, 28–31, 35, 36, 50, 61–63, 67, 68, 104–109

Условные обозначения

- контрольный отрезок 1000 мм натуры: по нему проверяют печать 1:1
- отметка уровня, м: ±0,000 — чистый пол жилых помещений
- А — марка развёртки: буква стены, стрелка — взгляд
- О1 — марка отделки по реестру отделки альбома
- выноска узла: над полкой — узел, под полкой — лист

Допущения и предложения на листе

Основа листа: размеры помещений и положение проёмов введены заказчиком в брифе, на объекте не замерены (К-1); высота потолка 2700 мм — по брифу заказчика, не замерена (К-2); толщины стен приняты по брифу: наружные 200 мм, внутренние 150 мм — не обмерены (К-1); тип дома монолитный, перекрытие 200 мм — по брифу заказчика, документов нет (К-3); планировка (стены, проёмы, объединение кухни и гостиной, расширение санузла) — по брифу без обмера и плана БТИ (К-7); разрешённая мощность 10 кВт принята, ТУ не переданы (К-8); вентканалы приняты, в брифе не заданы (К-9); подрайон климата не задан — принят не северный (жилые от 2,5 м) (К-10).
См. лист открытых вопросов (лист 6, записи К-1–К-3, К-7–К-10).

Общие указания

1. Рабочие чертежи интерьера разработаны на основании задания на проектирование и обмерного плана (лист 21). Объект: Квартира 56 м², ЖК «Северный парк», Москва; автор проекта — Кырлан Александр Сергеевич; общая площадь 56,37 м², жилая 42,98 м², помещений 5.
2. Рабочие чертежи выполнены в соответствии с заданием на проектирование и нормативными документами, перечисленными в п. 4.
3. Открытые вопросы, принятые допущения и конфликты между разделами, не снятые к выпуску комплекта, сведены в таблицы на листах 6, 7. До ответа по пункту таблицы показанное на указанном там листе — допущение, а не утверждённое решение: комплект по этим листам предварительный.
4. Нормативные документы, на которые есть ссылки в листах комплекта: ГОСТ Р 21.101-2026; ГОСТ 21.501-2018; ГОСТ 2.302-68; ГОСТ 2.303-68; ГОСТ 2.304-81; ГОСТ 2.307-2011; СП 54.13330.2022; СП 71.13330.2017; СП 73.13330.2016; ПУЭ (7-е изд.), гл. 1.8, 7.1; ГОСТ Р 50571.7.701-2024; СанПиН 1.2.3685-21; ГОСТ 2.702; ГОСТ 2.755; ГОСТ 21.110-2013; ГОСТ 21.601; ГОСТ 13996-2019; ГОСТ 23166-2021; ГОСТ 31173-2016; ГОСТ 31565-2012; ГОСТ 32414-2013; ГОСТ 32415-2013; ГОСТ 32614-2012; ГОСТ Р 56387-2018; СП 15.13330; СП 29.13330.2011; СП 30.13330.2020; СП 51.13330.2011; СП 131.13330; СП 163.1325800.2014; СП 256.1325800.2016. Документы из ведомости ссылочных документов здесь не повторяются.
5. За отметку ±0,000 принят уровень чистого пола жилых помещений квартиры (относительная отметка; абсолютная — по проекту дома). Отметка чистого пола мокрых помещений — −0,015. Размеры — в миллиметрах, отметки — в метрах, площади — в м²; высоты установки Н от чистого пола своего помещения до оси изделия.
6. Несущие конструкции, общедомовые стояки, вентиляционные каналы и инженерные сети дома настоящим комплектом не изменяются.
7. Трассы инженерных сетей на листах — принципиальные. Расчёты электрических нагрузок и токов КЗ, гидравлики, воздухообмена, освещённости и нагрузок на перекрытие выполняются в проектах ЭОМ, ВК, ОВ и КР организацией с допуском СРО; фактические трассы до закрытия отделкой фиксируются исполнительными схемами.
8. Стиль интерьера — Джапанди. Палитра проекта: основной 60 % — NCS S 0804-Y30R «S 0804-Y30R», Tikkurila F485 «Damask»; дополнительный 30 % — Tikkurila X447 «Sea Smoke», Tikkurila V484 «Driftwood», NCS S 2005-Y30R «S 2005-Y30R»; акцент 10 % — Farrow & Ball No. 298 «Bancha», NCS S 5010-G70Y «S 5010-G70Y», NCS S 7005-Y20R «S 7005-Y20R». Коды цвета — по веерам производителей; цвет утверждается по выкрасу на объекте при освещении проекта.
9. Площади поверхностей — по чистым граням стен до отделки: стены = периметр × высоту от чистого пола помещения до низа потолка минус проёмы (облицовка плиткой — до верха облицовки); плинтус = периметр минус дверные проёмы; пол и потолок — по площади помещения. Количество плиток — по раскладке. Способ один для всех листов комплекта (ведомость отделки, колерная карта, раскладка плитки, развёртки).
10. Марки: стены помещения на всех листах — А (верхняя по плану), Б (правая), В (нижняя), Г (левая); марка отделки О — одна на весь альбом; реестр марок отделки (с позициями колерной карты той же отделки) и марки позиций по видам — на листе 82.
11. Развёртки стен выполнены по всем помещениям для стен с электроточками, мебелью, декором и отделкой: санузлы и кухонный фронт — в М 1:25, остальные стены — в М 1:25; расположение развёрток и узлов — на листе 83, узлы — на листе 102.
12. Перечень скрытых работ, на которые составляются акты освидетельствования (форма по приказу Минстроя России № 344/пр): гидроизоляция пола и стен мокрых помещений (с тестом проливом); стяжка пола (толщина, прочность, влажность основания); скрытая электропроводка (за потолком и в штробах стен; условия штробления — в следующем пункте); трубопроводы водоснабжения и канализации до закрытия (опрессовка, уклоны); закладные и усиления под подвесные приборы, мебель и тяжёлый декор, рамы инсталляций; короба дверей скрытого монтажа до штукатурки; каркасы ГКЛ потолков, коробов и перегородок до обшивки.
13. Скрытая электропроводка: за потолком и в штробах стен. Штробы в стенах выполняются только после технического заключения о несущих конструкциях; до заключения несущие стены не определены, и все стены считаются несущими; объём штроб — в ведомости объёмов работ, строка «Штробы в стенах» (вертикальные спуски; объём не меньше фактического, горизонтальные трассы — по исполнительной схеме).
14. Критерии приёмки: допуски отделочных покрытий — по СП 71.13330.2017; испытания систем водоснабжения и канализации — по СП 73.13330.2016 до закрытия трасс; приёмо-сдаточные испытания электроустановки — по ПУЭ, гл. 1.8, с протоколом электролаборатории.
15. Осознанные отступления от ГОСТ Р 21.101-2026, принятые в комплекте: номер листа и число листов («Листов») указаны на каждом листе; на масштабных листах в основной надписи указан фактический масштаб и дан контрольный отрезок 1000 мм; развёртки стен выполнены в М 1:25 (ГОСТ 21.507-81 — 1:50…1:500) ради читаемости привязок; размерные числа и марки элементов (Д-1, ОК-1, О6) кеглем 2,5 мм, номера помещений — в кружке Ø 8 мм (канон — 3,5 мм и Ø 12 мм): так насыщенные листы А3 читаются без наложений надписей.
16. Графы «Пров.», «Н. контр.», «Утв.» основной надписи заполняются при согласовании комплекта с заказчиком; до согласования комплект подписывает автор проекта (графа «Разраб.»).

Изм.	Кол.уч	Лист	№ док.	Подп.	Дата	ГД-2026-011-АИ		
						Квартира 56 м² ЖК «Северный парк», Москва		
Разраб.		Кырлан А.С.			13.11.26	Дизайн-проект интерьера	Стадия: РП	Лист: 5 / Листов: 119
Пров.								
ГИП								
Н. контр.						Общие данные М б/м	Кырлан Александр Сергеевич	
Утв.								

выпуск 13.11.2026 № eb78110814f · стр. 5 из 139

Открытые вопросы, принятые допущения и конфликты. Лист 1 из 2

Сводка по реестрам координации (стартовое совещание 19.10.2026)

Комплект предварительный по пунктам этих таблиц. Пока по пункту нет ответа или решения, показанное на указанном листе — допущение проектировщика, а не утверждённое решение.
Сводка: открытых вопросов — 12 (из них ждут факта объекта — 8: контрольного обмера, обследования или документа); изменений в реестре — 3, из них без подписи — 1.
Пункты, ответ на которые лежит на объекте, а не за столом проектировщика (графа «Вид», строка «Ждёт»), собраны на листе «Задание на контрольный обмер и обследование» (листы 8–11): что и где замерить, с какой точностью и чем подтвердить. Пункты, ждущие решения человека, на объекте не закрываются.

Открытые вопросы и принятые допущения

№	Формулировка	Вид	Кто решает	Если решения нет	Лист, где это проявляется
К-1	Размеры помещений, толщины стен (наружные 200 мм, перегородки 150 мм) и положение проёмов введены заказчиком в бриф заказчика (site-brief-wizard, 01.08.2026): контрольный обмер на объекте не выполнялся, обмерного плана и плана БТИ в материалах нет; площадь по брифу 56 м², сумма помещений по чистым размерам брифа 56.37 м². От этого зависят все размеры альбома, площади, заказ материалов и изделий. Выполнить контрольный обмер.	Непонятно Ждёт: обмера	Архитектор-планировщик	все размеры альбома остаются по брифу заказчика и не считаются замеренными; заказ изделий по ним не ведётся	л. 21 — Обмерный план л. 25 — План дверей и ведомость заполнения проёмов
К-2	Высота потолка 2700 мм указана заказчиком в брифе, на объекте не замерена. От неё зависят вертикальные размеры альбома (развёртки, шкафы, перегородки, объёмы работ). Замерить высоту на объекте.	Непонятно Ждёт: обмера	Архитектор-планировщик	вертикальные размеры альбома остаются по брифу и не считаются замеренными	л. 21 — Обмерный план
К-3	Тип дома (монолитный) и толщина перекрытия 200 мм указаны заказчиком в брифе; проект дома, план БТИ и техническое заключение о несущих конструкциях не переданы. Несущие стены и допустимость демонтажа определяются только по этим документам или по обследованию.	Отсутствует Ждёт: документа, обследования	Архитектор-планировщик	все существующие стены считаются несущими; демонтаж и штробление в них не выполняются до технического заключения	л. 21 — Обмерный план л. 22 — План демонтажа и монтажа перегородок
К-4	Положение и диаметры стояков (канализации, холодной воды) указаны заказчиком в брифе, не замерены; врезки, краны и счётчики не описаны. От стояков зависят трассы водопровода и канализации, привязки выводов и уклоны. Замерить на объекте.	Непонятно Ждёт: обмера	Инженер ВК (вода, канализация)	трассы и привязки выводов остаются по положению стояков из брифа и не считаются замеренными	л. 43 — План выводов сантехники л. 44 — Схема разводки водопровода и канализации
К-5	Новые перегородки заданы заказчиком в брифе положением, материалом и толщиной; конструкция (система, число слоёв, каркас, звукоизоляция, Rw) выбрана исполнителем по каталогам. Утвердить конструкцию перегородок или задать другую. Толщина по брифу и стена на плане расходятся: П-1 — 100 мм по брифу, П-3 — 120 мм по брифу, а план брифа построен со стенами 150 мм — на плане и в привязках стена 150. Решить, что верно: толщина по брифу (тогда соседние помещения шире, площади и привязки пересчитать) или 150 мм с отделкой.	Спорно Ждёт: решения	Архитектор-планировщик	конструкция перегородок остаётся по решению исполнителя со знаком «предложено»	л. 22 — План демонтажа и монтажа перегородок
К-6	Цвета названы заказчиком в брифе словами (тёплый белый, натуральное дерево, серо-зелёный). Исполнитель перевёл их в коды по веерам стиля джапанди: стены NCS S 0804-Y30R, потолки Tikkurila F485 Damask, второй план Tikkurila X447 Sea Smoke и V484 Driftwood, акценты Farrow & Ball No. 298 Bancha и NCS S 5010-G70Y (по комнатам). Выкрасы на объекте не делались. Утвердить коды по выкрасам. Матовость: в брифе в «не нравится» — «Глянец, холодный белый», поэтому стены матовые (в кухне-гостиной и прихожей — матовая моющаяся краска вместо полуматовой, класс мойки — по ведомости отделки); подтвердить вместе с кодами.	Спорно Ждёт: решения	Колорист-комплектатор	коды — предложение исполнителя; краску не закупать до выкрасов	л. 62 — Колерная карта
К-7	Планировка принята по брифу заказчика: положение существующих стен и проёмов, объединение кухни с гостиной (демонтаж С-1), расширение санузла (демонтаж С-2, перегородка П-1) введены в мастер брифа без обмерного плана и плана БТИ. Расстановка мебели и кухни, рабочее место в спальне, антресоль в прихожей — предложение исполнителя по этой планировке. Нужны план БТИ и контрольный обмер; до них планировочное решение — предварительное.	Непонятно Ждёт: документа	Архитектор-планировщик	расстановка остаётся предложением; мебель на заказ (кухня, шкафы) не заказывать	л. 21 — Обмерный план л. 22 — План демонтажа и монтажа перегородок л. 27 — План расстановки мебели
К-8	Разрешённая мощность квартиры по ТУ в брифе не указана; принята 10 кВт (квартира с электроплитой, монолитный дом). Передать ТУ или справку УК.	Отсутствует Ждёт: документа	Инженер-электрик	щит и группы рассчитаны на 10 кВт; при меньших ТУ пересчёт групп варочной панели и духового шкафа	л. 37 — Однолинейная схема щита
К-9	Вентканалы в брифе не показаны: принято два канала — ВК-1 в санузле у стояков (стена А) и ВК-2 у стены В бывшей кухни. От них зависят вытяжка санузла, вытяжка над плитой (до обмера — рециркуляция) и короба потолка. Замерить положение и сечение на объекте.	Отсутствует Ждёт: обмера	Инженер ОВ	вытяжка кухни — рециркуляционная; вентилятор санузла по месту ВК-1 после обмера	л. 41 — План вентиляции л. 43 — План выводов сантехники
К-10	Климатический подрайон (СП 131.13330) не задан: принят не северный — жилые комнаты и кухня под потолком от 2,5 м (СП 54, п. 5.12); в IA, IБ, IГ, IД, IVA — от 2,7 м.	Отсутствует Ждёт: документа	Архитектор-планировщик	отметки потолков жилых — по 2,5 м; при северном подрайоне уровни ниже 2,7 м пересчитать до заказа каркаса	л. 53 — План потолков

						ГД-2026-011-АИ		
						Квартира 56 м² ЖК «Северный парк», Москва		
Изм.	Кол.уч	Лист	№ док.	Подп.	Дата	Дизайн-проект интерьера	Стадия	Лист	Листов
Разраб.		Кырлан А.С.			13.11.26		РП	6	119
Пров.									
ГИП									
Н. контр.						**Открытые вопросы, принятые допущения и конфликты. Лист 1 из 2** М б/м	**Кырлан Александр Сергеевич**		
Утв.									

выпуск 13.11.2026 № eb7810814f · стр. 6 из 139

Открытые вопросы, принятые допущения и конфликты. Лист 2 из 2

Сводка по реестрам координации (стартовое совещание 19.10.2026)

Открытые вопросы и принятые допущения (продолжение)

№	Формулировка	Вид	Кто решает	Если решения нет	Лист, где это проявляется
К-11	Мойка кухонная П1 (пом. 1 «Гостиная-кухня»), выпуск К1-1 Ø50: до стояка Ст К1-1 15,58 м через пом. 5 «Прихожая», перепад 390 мм — короб 470×110 над полом через чужие помещения (их проёмы, мебель, проход) не построить. Решить: (а) насосная установка (КНС) под мойкой/прибором с напорной трубой Ø32 к стояку (по паспорту, обслуживаемый люк); (б) подиум кухонной зоны на 470 мм с трубой под ним; (в) перенос прибора ближе к стояку Ст К1-1. Решение меняет кухню (модули, цоколь, точки ЭОМ) — за автором с заказчиком.	Спорно Ждёт: решения	Инженер ВК (вода, канализация)	выпуск К1-1 и кухню в части мойки не выполнять до решения; остальное — по листам	л. 44 — Схема разводки водопровода и канализации л. 43 — План выводов сантехники
К-12	Помещение «Спальня»: выключатель основного света L1 (S1) не у входа — у двери Д-3 со стороны ручки свободного места нет (проём в 100 мм от угла, мебель у двери, чужие точки или выключатель общий с соседним помещением; расстановка мебель и двери не двигает). Варианты: (а) петли на другую сторону — ручка уходит от угла, выключатель встаёт у ручки; (б) шкаф или тумбу у двери сдвинуть на 300 мм — место освобождается; (в) беспроводной выключатель на клее у ручки (реле в подрозетнике ближней стены) — по согласованию с заказчиком; (г) оставить как есть (S1): рука дальше 350 мм от ручки.	Спорно Ждёт: решения	Инженер-электрик	выключатель L1 остаётся на месте (S1); закладные под выключатель у двери не делать до решения	л. 34 — План выключателей и схема включения

Изменения проекта после выпуска листов (реестр изменений)

№	Дата	Лист	Было	Стало	Кто решил, подпись
ИЗ-1	30.10.2026	л. 27 — План расстановки мебели л. 25 — План дверей и ведомость заполнения проёмов л. 53 — План потолков л. 33 — План освещения л. 87 — Развёртка стены В. Гостиная-кухня (пом. 1)	Гостиная-кухня: вход Д-2 (стена В, 3700…4600) упирался в спинку дивана Гс2, слева проход между консолью Гс5 (1600…3400) и креслом Гс4 — 575 мм, справа 175 мм до стены Б. Остров потолка У2 не центрирован на стол Кх11 (зазор 100 / 450), подвесы — по столу. Детская: стол Дт3 вплотную к стене В над радиатором РО-3, примечание «прибор в корпусе не решён».	Д-2 — петли у правого откоса, консоль Гс5 — смещение 700…2500, кресло Гс4 — у 2100…2850: проход от двери к кухне 975 / 825 мм. Остров У2 — вставка А340/В1910/С2210/D1340 (центр по столу), точка ленты Св41 — х 3300. Стол Дт3 — у стены Б торцом к окну (х 2775…3375, у 5550…6750), стул Дт4 — х 2200, у 5900; радиатор РО-3 открыт. Знак «**» у Гс5, Гс4, Дт3 до подписи автора.	Утверждено: Кырлан А.С., 12.11.2026. Предложил: исполнитель.
ИЗ-2	10.11.2026	л. 27 — План расстановки мебели л. 65 — План текстиля и декора	Стол Дт3 (детская, пом. 3) стоял вплотную к дверному проёму Д-4 в стене Б: край стола у 5550 мм = край проёма.	Стол Дт3 сдвинут вдоль стены Б на 250 мм от двери: у 5800…6400 мм (было 5550…6150), х 2000…3200 прежний; зазор от проёма Д-4 250 мм. Стул Дт4 сдвинут вместе со столом: у 6150…6650 (было 5900…6400), х 2200 прежний; до стены С остаётся 100 мм. Розетки Р11, LAN2 у стола на стене С (смещения 2400 и 2500) не тронуты. Стол Дт3 остаётся предложением проектировщика.	Утверждено: Кырлан А.С., 12.11.2026. Предложил: исполнитель.
ИЗ-3	12.11.2026	л. 65 — План текстиля и декора л. 67 — Ведомость текстиля л. 68 — Ведомость декора. Схемы развески	Разбор двух критиков по кадрам: «стерильный шоурум, жизни нет»; ванна Сн1 в кадре без смесителя — в наименовании прибора смеситель не назван. Санузел без текстиля и предметов; на столах, консоли и тумбах нет ни одной вещи; в прихожей — только зеркало над скамьёй; на диване и кроватях по 5 декоративных подушек.	Ванна Сн1 — «акриловая 1700×750, смеситель настенный». Санузел: банные и ручные полотенца на полотенцесушителе Сн5 (Т20, Т21), коврик 800×450 у бортика ванны (Т22; вне полотна двери Д-5), ваза с сухой веткой на полке короба инсталляции (ДК9). Прихожая: графика «энсо» 400×560 в простенке стены Г (ДК10); дорожка и консоль не заданы — свободный пол в зонах открывания пяти дверей, стены заняты щитами, домофоном и выключателями. Гостиная-кухня: книги и свеча на журнальном столике (ДК11), керамика и настольная лампа на консоли Гс5 (ДК12, ДК13), керамика на столешнице кухни (ДК14). Спальня: книги на тумбе Сп2 (ДК15), шеффлера в углу у окна (ДК16), рабочая лампа на столе Сп5 (ДК17). Детская: рабочая лампа на столе Дт3 (ДК18). Декоративных подушек — по 4 на диван и кровати (Т17, Т4, Т10: 3 → 2). Цвета — из палитры джапанди проекта: олива Bancha и S 5010-G70Y, песочный S 2005-Y30R, тёплый белый Damask. Знак «**» у позиций до подписи автора.	Не утверждено: подписи нет. решение исполнителя; предложение проектировщика, на утверждение А. С. Кырлана

Примечания

1. Номера листов — по ведомости рабочих чертежей комплекта (лист «Общие данные»).
2. Графа «Если решения нет» показывает состояние решения на листах; влияние на сроки и стоимость по пунктам не оценивалось.
3. Пункт, по которому принято решение, при следующем выпуске комплекта из таблиц исключается.

						ГД-2026-011-АИ	
						Квартира 56 м² ЖК «Северный парк», Москва	
Изм.	Кол.уч	Лист	№ док.	Подп.	Дата	Дизайн-проект интерьера	Стадия: РП; Лист: 7; Листов: 119
Разраб.		Кырлан А.С.			13.11.26	**Открытые вопросы, принятые допущения и конфликты. Лист 2 из 2** М б/м	**Кырлан Александр Сергеевич**
Пров.							
ГИП							
Н. контр.							
Утв.							

Задание на контрольный обмер и обследование. Лист 1 из 4

ПРЕДВАРИТЕЛЬНО · не для производства работ · открыто пунктов: 13 (реестр — л. 6, 7)

Что замерить, вскрыть и получить до заказа материалов и изделий

Задание собрано из открытых вопросов, ответ на которые лежит на объекте или в документах, а не за столом проектировщика. Пока факт не получен, размер, материал или положение на листах — допущение (знак «*»), а не замер.
Сводка: на объекте — 16 (до демонтажа — 14; после демонтажа — 2); документом и при закупке — 4; из допущений в данных и на листах — 16, из них без вопроса в реестре — 4. Закрываются вопросы: К-1–К-4, К-7–К-10 (8). Вопросы, ждущие решения человека, задание не закрывает — они решаются по реестру открытых вопросов.

Условия проведения

Порядок работ	Приёмы и точность	Кто присутствует	Если факт не совпал с проектом
1. До демонтажа — существующее состояние: контур, диагонали, высоты, проёмы, оси стояков, ниши и конструкции, которые видны. 2. После демонтажа, до черновых работ — то, что закрывали отделка и короба: основание стен, фактические толщины, углы, узлы. 3. Документы и данные закупки — не на объекте: к сроку из последней таблицы, от них зависят привязки и заказ. Что заказывается по размеру из задания, до закрытия пункта не заказывают: сроки изготовления — по графику закупок прораба.	Обход по часовой стрелке от входа: стены, проёмы, потолок, коммуникации (стояки, щиток, вентканалы), особенности (ниши, короба, выступы). Размеры записывают в мм; сумма участков равна общему размеру, при цепочке длиннее трёх участков ставят проверочный (общий) размер. Диагонали каждого помещения; если две диагонали различаются на 5 мм и больше, разницу подписывают на плане. Потолок — в нескольких точках: центр, углы, у проёмов. Проём — ширина, высота, глубина откоса, привязка к ближайшим углам, высота подоконника. Допустимая погрешность прибора — 2–3 мм на метр; размеры округляют кратно 5 мм; два контрольных промера одного размера не должны расходиться более чем на 2 %. Допуск по пункту — в графе «Точность». План БТИ обмер не заменяет.	Прораб (отвечает за проведение) — назначает день и порядок обхода, открывает объект и освобождает помещения, ведёт это задание и реестр изменений. Архитектор — выполняет обмер, составляет акт контрольного обмера и подписывает результаты по размерам и конструкциям. Владельцы вопросов присутствуют при пунктах своего раздела или принимают результат до заказа: Инженер ВК (вода, канализация) — К-4; Инженер-электрик — К-8; позиции О-1; Инженер ОВ — К-9; позиции О-2; Отделочник — позиции О-15, О-16. Технадзор — при вскрытиях и обследованиях: фото с рулеткой до закрытия. Заказчик или его представитель — передаёт документы (план БТИ, проект дома, технические условия, паспорта), подписывает акт. Проектных решений на обмере не принимают: обмер даёт факт, решения — по реестру открытых вопросов (листы 6–7).	1. В пределах допуска пункта — принимается измеренное значение, лист перевыпускается, знак «*» снимается. 2. Больше допуска или контрольные промеры расходятся более чем на 2 % — промер повторяют; не подтвердилось — запись в реестр изменений (дата, лист, было, стало, кто решил, подпись), работы в этом месте не начинают. 3. Затронуты несущая стена, стояк, вентканал или мокрая зона — сразу владельцу раздела и ГИПу (главному инженеру проекта); между разделами не больше двух кругов, затем решает ГИП. 4. На объекте устно ничего не согласуется: каждое решение — записью в реестр с подписью.

Этап 1. До демонтажа

№	Где	Способ	Что сделать	Кто выполняет	Точность	Что пересчитается в альбоме	Чем подтверждается	Закрывает вопросы реестра
О-1	Вход в квартиру или лестничная клетка; место щита на плане	Обмер	Существующий щиток и счётчик электроэнергии: место и габарит ниши, состояние ввода, марка и сечение вводного кабеля, наличие вводного автомата и УЗО, пломбы.	Архитектор	±5 мм	Ниша и место щита на листах; вводной кабель и аппараты на однолинейной схеме; расстояния до первых групп. Листы: л. 37 — Однолинейная схема щита	акт контрольного обмера; фото с рулеткой и привязкой к стене или углу	Вопроса в реестре нет: Альбом принимает щит и ввод без осмотра. Результат принимает: Инженер-электрик
О-2	Гостиная-кухня (пом. 1), Спальня (пом. 2), Детская (пом. 3); у окон	Обмер	Положение стояков отопления (подающий и обратный) от граней стен, диаметры, наличие запорной арматуры; существующие радиаторы: число секций, межосевое расстояние, подводки. В данных стояков отопления нет — лист отопления выводит их условно у откоса окна, радиаторы — «принципиально, по расчёту».	Архитектор	±5 мм	План отопления: места стояков и подводок, привязки радиаторов; подбор радиаторов по теплотехническому расчёту; радиаторы и узлы подключения в ВОР и спецификации. Листы: л. 42 — План отопления	акт контрольного обмера; фото с рулеткой и привязкой к стене или углу	Вопроса в реестре нет: Альбом принимает положение стояков и радиаторов отопления без обмера. Результат принимает: Инженер ОВ
О-3	Вся квартира, все помещения; обход по часовой стрелке от входа	Обмер	Контрольный обмер всех помещений: чистые размеры, диагонали, толщины стен (по брифу 200 мм наружные и 150 мм внутренние), положение и размеры существующих проёмов дверей и окон, подоконники, высота проёмов.	Архитектор	±5 мм; диагонали — разница от 5 мм подписывается	Чистые размеры и площади помещений, толщины стен, положение проёмов; размеры, по которым заказываются материалы и изделия. Листы: л. 21 — Обмерный план л. 25 — План дверей и ведомость заполнения проёмов	акт контрольного обмера	К-1 Результат принимает: Архитектор

Допущения и предложения на листе
Основа листа: размеры помещений и положение проёмов введены заказчиком в брифе, на объекте не замерены (К-1); высота потолка 2700 мм — по брифу заказчика, не замерена (К-2); толщины стен приняты по брифу: наружные 200 мм, внутренние 150 мм — не обмерены (К-1); тип дома монолитный, перекрытие 200 мм — по брифу заказчика, документов нет (К-3); планировка (стены, проёмы, объединение кухни и гостиной, расширение санузла) — по брифу без обмера и плана БТИ (К-7); разрешённая мощность 10 кВт принята, ТУ не переданы (К-8); вентканалы приняты, в брифе не заданы (К-9); подрайон климата не задан — принят не северный (жилые от 2,5 м) (К-10).
См. лист открытых вопросов (лист 6, записи К-1–К-3, К-7–К-10).

Изм.	Кол.уч	Лист	№ док.	Подп.	Дата
Разраб.		Кырлан А.С.			13.11.26
Пров.					
ГИП					
Н. контр.					
Утв.					

ГД-2026-011-АИ

Квартира 56 м²

ЖК «Северный парк», Москва

Дизайн-проект интерьера

Стадия	Лист	Листов
РП	8	119

Задание на контрольный обмер и обследование.
Лист 1 из 4
М б/м

Кырлан Александр Сергеевич

выпуск 13.11.2026 № eb7810814f · стр. 8 из 139

Задание на контрольный обмер и обследование. Лист 2 из 4

Что замерить, вскрыть и получить до заказа материалов и изделий

Этап 1. До демонтажа (продолжение)

№	Где	Способ	Что сделать	Кто выполняет	Точность	Что пересчитается в альбоме	Чем подтверждается	Закрывает вопросы реестра
О-4	Все помещения квартиры	Обмер	Высота потолка в каждом помещении в нескольких точках: центр, углы, у проёмов. По брифу 2700 мм.	Архитектор	±5 мм	Вертикальные размеры альбома: развёртки, перегородки, шкафы, объёмы работ. Листы: л. 21 — Обмерный план	акт контрольного обмера	К-2 Результат принимает: Архитектор
О-5	Стены по плану демонтажа; перекрытие в зоне новых перегородок	Обследование	Обследование конструкций: материал и несущая способность стен, подлежащих демонтажу, конструкция перекрытия.	специализированная организация по договору с заказчиком	по методике организации	План демонтажа и монтажа; основания демонтажа (техзаключение). Листы: л. 21 — Обмерный план л. 22 — План демонтажа и монтажа перегородок	техническое заключение	К-3 Результат принимает: Архитектор
О-6	Санузел (пом. 4): Ст К1-1*, Ст В1-1*; наличие стояка ГВС, арматуры и счётчиков — по всей квартире	Обмер	Положение стояков Ст К1-1*, Ст В1-1*: привязка осей от граней стен, диаметры, размеры короба и люков. Стояк горячей воды Т3 в данных не задан, на листах ВК принят рядом с Ст В1-1*: выяснить, есть ли он в доме, и где. Отключающая арматура и счётчики воды на вводах: положение, тип, пломбы управляющей компании. Сверить до разметки выводов.	Архитектор	±5 мм	Привязки выводов воды и канализации на планах выводов и разводки; расстояние розеток до стояка; места люков 300 × 400 мм; трассы Т3 и полотенцесушители (водяной или электрический); узлы ввода в спецификации ВК (краны, фильтры, счётчики). Трассы В1, Т3, К1, привязки выводов сантехники, уклоны канализации, короба стояков. Листы: л. 43 — План выводов сантехники л. 44 — Схема разводки водопровода и канализации	акт контрольного обмера; фото с рулеткой и привязкой к стене или углу	К-4 Результат принимает: Инженер ВК (вода, канализация)
О-7	По месту	Обмер	Подтвердить на объекте принятое: планировка (стены, проёмы, объединение кухни и гостиной, расширение санузла) — по брифу без обмера и плана БТИ	Архитектор	±5 мм	Листы, где используется принятая величина. Листы: л. 2–5 — Общие данные	акт контрольного обмера	К-7 Результат принимает: Архитектор
О-8	По месту	Обмер	Подтвердить на объекте принятое: вентканалы приняты, в брифе не заданы	Архитектор	±5 мм	Листы, где используется принятая величина. Листы: л. 2–5 — Общие данные	акт контрольного обмера	К-9 Результат принимает: Инженер ОВ
О-9	санузел, кухня	Обмер	Положение и сечение вентканалов, тяга.	исполнитель	±10 мм	план вентиляции, потолки, вытяжка кухни Листы: л. 41 — План вентиляции л. 43 — План выводов сантехники	акт контрольного обмера	К-9 Результат принимает: Инженер ОВ
О-10	По месту	Обмер	Подтвердить на объекте принятое: подрайон климата не задан — принят не северный (жилые от 2,5 м)	Архитектор	±5 мм	Листы, где используется принятая величина. Листы: л. 2–5 — Общие данные	акт контрольного обмера	К-10 Результат принимает: Архитектор
О-11	Гостиная-кухня (пом. 1): окно пом. 1, стена А, дверь пом. 1, стена В	Обмер	Окно пом. 1, стена А, дверь пом. 1, стена В: положение (привязки к ближайшим углам), ширина, высота, высота подоконника, глубина откоса. Принято в проекте: окно: положение, ширина, высота и подоконник — по брифу заказчика, не замерены; ограждение 900 мм — предложение исполнителя, Петли у правого откоса (х 4600): открытое полотно стоит у стены Б, вошедший идёт влево к кухне; при петлях слева полотно запирало вход в карман между собой, диваном Гс2 и стеной Б. ИЗ-N см. реестр..	Архитектор	±5 мм	Проёмы на обмерном плане и в ведомости проёмов; откосы и оконные работы в ВОР; привязки мебели и выводов к проёмам. Листы: л. 21 — Обмерный план л. 25 — План дверей и ведомость заполнения проёмов	акт контрольного обмера; фото с рулеткой и привязкой к стене или углу	К-1 Результат принимает: Архитектор

Допущения и предложения на листе

Основа листа: размеры помещений и положение проёмов введены заказчиком в брифе, на объекте не замерены (К-1); высота потолка 2700 мм — по брифу заказчика, не замерена (К-2); толщины стен приняты по брифу: наружные 200 мм, внутренние 150 мм — не обмерены (К-1); тип дома монолитный, перекрытие 200 мм — по брифу заказчика, документов нет (К-3); планировка (стены, проёмы, объединение кухни и гостиной, расширение санузла) — по брифу без обмера и плана БТИ (К-7); разрешённая мощность 10 кВт принята, ТУ не переданы (К-8); вентканалы приняты, в брифе не заданы (К-9); подрайон климата не задан — принят не северный (жилые от 2,5 м) (К-10).

Знак «*» — принято, не замерено и не подтверждено (замерить на объекте): К-4: Ст К1-1 — положение стояка канализации — по брифу заказчика, не замерено; Ст В1-1 — положение стояка холодной воды — по брифу заказчика, не замерено.

См. лист открытых вопросов (лист 6, записи К-1–К-4, К-7–К-10).

Изм.	Кол.уч	Лист	№ док.	Подп.	Дата
Разраб.		Кырлан А.С.			13.11.26
Пров.					
ГИП					
Н. контр.					
Утв.					

ГД-2026-011-АИ

Квартира 56 м²

ЖК «Северный парк», Москва

Дизайн-проект интерьера

Стадия	Лист	Листов
РП	9	119

Задание на контрольный обмер и обследование.
Лист 2 из 4
М б/м

Кырлан Александр Сергеевич

выпуск 13.11.2026 № eb7810814f · стр. 9 из 139

Задание на контрольный обмер и обследование. Лист 3 из 4

ПРЕДВАРИТЕЛЬНО · не для производства работ · открыто пунктов: 13 (реестр — л. 6, 7)

Что замерить, вскрыть и получить до заказа материалов и изделий

Этап 1. До демонтажа (продолжение)

№	Где	Способ	Что сделать	Кто выполняет	Точность	Что пересчитается в альбоме	Чем подтверждается	Закрывает вопросы реестра
О-12	Спальня (пом. 2): окно пом. 2, стена А, дверь пом. 2, стена В	Обмер	Окно пом. 2, стена А, дверь пом. 2, стена В: положение (привязки к ближайшим углам), ширина, высота, высота подоконника, глубина откоса. Принято в проекте: окно: положение, ширина, высота и подоконник — по брифу заказчика, не замерены, проём в существующей стене между пом. 2 и 5: положение и ширина — по брифу заказчика, не замерены.	Архитектор	±5 мм	Проёмы на обмерном плане и в ведомости проёмов; откосы и оконные работы в ВОР; привязки мебели и выводов к проёмам. Листы: л. 21 — Обмерный план л. 25 — План дверей и ведомость заполнения проёмов	акт контрольного обмера; фото с рулеткой и привязкой к стене или углу	К-1 Результат принимает: Архитектор
О-13	Детская (пом. 3): окно пом. 3, стена В	Обмер	Окно пом. 3, стена В: положение (привязки к ближайшим углам), ширина, высота, высота подоконника, глубина откоса. Принято в проекте: окно: положение, ширина, высота и подоконник — по брифу заказчика, не замерены.	Архитектор	±5 мм	Проёмы на обмерном плане и в ведомости проёмов; откосы и оконные работы в ВОР; привязки мебели и выводов к проёмам. Листы: л. 21 — Обмерный план л. 25 — План дверей и ведомость заполнения проёмов	акт контрольного обмера; фото с рулеткой и привязкой к стене или углу	К-1 Результат принимает: Архитектор
О-14	Прихожая (пом. 5): дверь пом. 5, стена В	Обмер	Дверь пом. 5, стена В: положение (привязки к ближайшим углам), ширина, высота, толщина стены в проёме. Принято в проекте: входная дверь: положение и ширина проёма — по брифу заказчика, не замерены.	Архитектор	±5 мм	Проёмы на обмерном плане и в ведомости проёмов; привязки мебели и выводов к проёмам. Листы: л. 21 — Обмерный план л. 25 — План дверей и ведомость заполнения проёмов	акт контрольного обмера; фото с рулеткой и привязкой к стене или углу	К-1 Результат принимает: Архитектор

Этап 2. После демонтажа, до черновых работ

№	Где	Способ	Что сделать	Кто выполняет	Точность	Что пересчитается в альбоме	Чем подтверждается	Закрывает вопросы реестра
О-15	Гостиная-кухня (пом. 1), Спальня (пом. 2), Детская (пом. 3), Санузел (пом. 4), Прихожая (пом. 5)	Обмер	Нивелировка плиты перекрытия и существующего пола после демонтажа покрытий: отметки в углах и по сетке, перепады по помещению, уклоны, отметки порогов (чистый пол в мокрых зонах принят -15 мм, 0 мм). Принятая толщина стяжки 33 мм, 50 мм и отметка чистого пола — расчётные, не от замера плиты.	Архитектор	±5 мм по отметке; ровность просвет под 2-метровой рейкой, горизонталь против 0,2 % длины помещения	Толщина стяжки и отметка чистого пола; уклоны к трапам и пороги; выпуски К1 относительно чистого пола (план разводки); объёмы стяжки и смеси в ВОР и спецификации. Листы: л. 57, 60 — План полов л. 44 — Схема разводки водопровода и канализации	акт контрольного обмера	Вопроса в реестре нет: Альбом принимает отметки плиты и толщину пирога пола без нивелировки. Результат принимает: Отделочник
О-16	Гостиная-кухня (пом. 1), Спальня (пом. 2), Детская (пом. 3), Санузел (пом. 4), Прихожая (пом. 5)	Обмер	Вертикаль и плоскостность стен: отклонение от вертикали по высоте стены (отвес или лазерный уровень), просвет под правилом 2 м, кривизна углов. Нужно там, где от стены зависит изделие: облицовка плиткой (пом. 4), штукатурка и окраска (пом. 1, 2, 3, 4, 5), встроенная мебель и кухня (пом. 1, 2, 3, 5).	Архитектор	до 1 мм на 2 м (правило и клиновой щуп); вертикаль — мм на высоту стены, отклонения подписываются на плане	Толщина штукатурки и расход смеси в ВОР и спецификации; раскладка плитки (подрезка у стен); зазоры и крепление встроенной мебели и кухни. Листы: л. 57–59 — Раскладка плитки л. 61 — Ведомость отделки помещений	акт контрольного обмера	Вопроса в реестре нет: Альбом принимает стены ровными и вертикальными без замера. Результат принимает: Отделочник

Допущения и предложения на листе

Основа листа: размеры помещений и положение проёмов введены заказчиком в брифе, на объекте не замерены (К-1); высота потолка 2700 мм — по брифу заказчика, не замерена (К-2); толщины стен приняты по брифу: наружные 200 мм, внутренние 150 мм — не обмерены (К-1); тип дома монолитный, перекрытие 200 мм — по брифу заказчика, документов нет (К-3); планировка (стены, проёмы, объединение кухни и гостиной, расширение санузла) — по брифу без обмера и плана БТИ (К-7); разрешённая мощность 10 кВт принята, ТУ не переданы (К-8); вентканалы приняты, в брифе не заданы (К-9); подрайон климата не задан — принят не северный (жилые от 2,5 м) (К-10).

См. лист открытых вопросов (лист 6, записи К-1–К-3, К-7–К-10).

Изм.	Кол.уч	Лист	№ док.	Подп.	Дата
Разраб.		Кырлан А.С.			13.11.26
Пров.					
ГИП					
Н. контр.					
Утв.					

ГД-2026-011-АИ

Квартира 56 м²

ЖК «Северный парк», Москва

Дизайн-проект интерьера

Стадия	Лист	Листов
РП	10	119

Задание на контрольный обмер и обследование.
Лист 3 из 4
М б/м

Кырлан Александр Сергеевич

выпуск 13.11.2026 № eb7810814f · стр. 10 из 139

Задание на контрольный обмер и обследование. Лист 4 из 4

Что замерить, вскрыть и получить до заказа материалов и изделий

Документы и данные закупки (не на объекте)

№	У кого, откуда	Способ	Что получить	К какому сроку	Что пересчитается в альбоме	Чем подтверждается	Закрывает вопросы реестра
О-17	Заказчик; управляющая компания или застройщик	Документ	Проект дома (разделы АР и КР) или план БТИ с указанием несущих конструкций; тип дома и конструкция перекрытия.	До начала демонтажных работ	Несущие стены на обмерном плане и плане демонтажа; допустимость демонтажа и новых проёмов; нагрузки от перегородок. Листы: л. 21 — Обмерный план л. 22 — План демонтажа и монтажа перегородок	копия документа	К-3 Результат принимает: Архитектор
О-18	вся квартира	Документ	Поэтажный план БТИ с экспликацией.	до демонтажа	обмерный план, план демонтажа и монтажа, расстановка мебели Листы: л. 21 — Обмерный план л. 22 — План демонтажа и монтажа перегородок л. 27 — План расстановки мебели	копия документа	К-7 Результат принимает: Архитектор
О-19	заказчик, УК	Документ	ТУ на электроснабжение или справка УК о разрешённой мощности и вводном автомате.	до сборки щита	вводной автомат, группы варочной панели и духового шкафа Листы: л. 37 — Однолинейная схема щита	копия документа	К-8 Результат принимает: Инженер-электрик
О-20	адрес объекта, СП 131.13330	Документ	Климатический подрайон по СП 131.13330 (по адресу объекта)	до заказа каркаса потолков	план потолков, разрезы, ведомость объёмов Листы: л. 53 — План потолков	копия документа	К-10 Результат принимает: Архитектор

Примечания

1. Подтверждение: акт контрольного обмера (дата, кто присутствовал, прибор, перечень промеров с результатами, подписи присутствующих); к акту — фото вскрытий и узлов и техническое заключение организации, выполнившей обследование.
2. Номера листов — по ведомости рабочих чертежей комплекта (лист «Общие данные»).
3. Пункт исключается из задания при следующем выпуске, когда акт подписан, значение внесено в проект и листы перевыпущены; знак «*» у величины снимается только замером.

Допущения и предложения на листе

Основа листа: размеры помещений и положение проёмов введены заказчиком в брифе, на объекте не замерены (К-1); высота потолка 2700 мм — по брифу заказчика, не замерена (К-2); толщины стен приняты по брифу: наружные 200 мм, внутренние 150 мм — не обмерены (К-1); тип дома монолитный, перекрытие 200 мм — по брифу заказчика, документов нет (К-3); планировка (стены, проёмы, объединение кухни и гостиной, расширение санузла) — по брифу без обмера и плана БТИ (К-7); разрешённая мощность 10 кВт принята, ТУ не переданы (К-8); вентканалы приняты, в брифе не заданы (К-9); подрайон климата не задан — принят не северный (жилые от 2,5 м) (К-10).
См. лист открытых вопросов (лист 6, записи К-1–К-3, К-7–К-10).

Изм.	Кол.уч	Лист	№ док.	Подп.	Дата
Разраб.		Кырлан А.С.			13.11.26
Пров.					
ГИП					
Н. контр.					
Утв.					

ГД-2026-011-АИ

Квартира 56 м²

ЖК «Северный парк», Москва

Дизайн-проект интерьера

Стадия	Лист	Листов
РП	11	119

Задание на контрольный обмер и обследование.
Лист 4 из 4
М б/м

Кырлан Александр Сергеевич

выпуск 13.11.2026 № eb7810814f · стр. 11 из 139

График закупок и работ. Лист 1 из 3

ПРЕДВАРИТЕЛЬНО · не для производства работ · открыто пунктов: 13 (реестр — л. 6, 7)

Что заказывать и когда не раньше чего: относительный порядок без дат; срок поставки — из данных или «не задан» с записью реестра

Лист не содержит дат: контрольного обмера, подписанных решений автора и договоров ещё нет, и любая дата была бы выдумана. Вместо календаря — порядок и условия: замер → решение и выбор изделия → заказ → срок поставки → работа, которую позиция блокирует.
Срок поставки печатается как срок, только если он задан в данных позиции. Нет — «срок поставки не задан» и ссылка на вопрос реестра о сроках; типовой диапазон практики стоит рядом как ориентир и заказывать по нему нельзя. Номера З-N и Р-N — строки этого листа, К-N — записи реестра открытых вопросов, О-N — позиции задания на контрольный обмер.

Закупки: что заказывается, от чего зависит заказ и какую работу блокирует

№	Позиция и где	1. Замер до заказа	2. Решение, выбор изделия, паспорт	3. Условие заказа	4. Срок поставки	5. Блокирует работу	Закрывает вопросы реестра
З-1	Двери скрытого монтажа с коробом под покраску в новой перегородке П-2**: Д-4 — 1 шт. пом. 3	О-13: обмер: Детская (пом. 3): окно пом. 3, стена В (К-1) О-3: обмер: Вся квартира, все помещения; обход по часовой стрелке от входа (К-1)	Новые перегородки заданы заказчиком в брифе положением, материалом и толщиной; конструкция (система, число слоёв, каркас, звукоизоляция, Rw) выбрана исполнителем по каталогам. (К-5)	После 1 и 2 и после получения срока у поставщика (вопроса о сроках нет); дата заказа — когда срок известен, не позднее чем за срок до начала Р-3.	срок поставки не задан (записи реестра нет) Ориентир практики (не срок поставщика): ≈ 30 дн.	Р-3 «перегородки ГКЛ»: коробку ставят в каркас перегородки до обшивки (работа по перегородкам); полотно навешивают после чистовой отделки стен	К-1, К-5
З-2	Двери скрытого монтажа с коробом под покраску в существующих проёмах: Д-2, Д-3, Д-5 — 3 шт. пом. 1, 2, 4	О-11: обмер: Гостиная-кухня (пом. 1): окно пом. 1, стена А, дверь пом. 1, стена В (К-1) О-12: обмер: Спальня (пом. 2): окно пом. 2, стена А, дверь пом. 2, стена В (К-1) О-3: обмер: Вся квартира, все помещения; обход по часовой стрелке от входа (К-1)		После 1 и 2 и после получения срока у поставщика (вопроса о сроках нет); дата заказа — когда срок известен, не позднее чем за срок до начала Р-6.	срок поставки не задан (записи реестра нет) Ориентир практики (не срок поставщика): ≈ 30 дн.	Р-6 «штукатурка»: короб ставят до штукатурки (коробку ставят на черновой стадии; полотно навешивают после чистовой отделки стен)	К-1
З-3	Кухонный гарнитур по проекту кухни: модули Кх1, Кх2, Кх3, Кх4, Кх5, Кх6, Кх7, Кх8, Кх9, Кх10 пом. 1			После 1 и 2 и после получения срока у поставщика (вопроса о сроках нет); дата заказа — когда срок известен, не позднее чем за срок до начала Р-16.	срок поставки не задан (записи реестра нет) Ориентир практики (не срок поставщика): 4–8 нед. от замера	Р-16 «кухня и мебель»: замер кухни — по готовым стенам после штукатурки или плитки, до чистового пола; производство идёт параллельно со стяжкой и отделкой	
З-4	Встраиваемая техника кухни: Кх1 холодильник, Кх6 посудомоечная машина, Кх8 вытяжка пом. 1			После 1 и 2 и после получения срока у поставщика (вопроса о сроках нет); дата заказа — когда срок известен, не позднее чем за срок до начала Р-16.	срок поставки не задан (записи реестра нет)	Р-16 «кухня и мебель»: паспорта и монтажные схемы — до изготовления модулей кухни: нишу и вентзазоры задаёт модель, а не типовая схема 60 см	
З-5	Стиральная машина: Сн4 (вертикальная загрузка 400 × 600 мм — условие закупки) пом. 4			После 1 и 2 и после получения срока у поставщика (вопроса о сроках нет); дата заказа — когда срок известен, не позднее чем за срок до начала Р-5.	срок поставки не задан (записи реестра нет)	Р-5 «черновая сантехника»: габарит и подводка — до закрытия люка и разводки	
З-6	Сантехнические приборы и инсталляции: П1, Сн1, Сн2, Сн3 пом. 1, 4	О-6: обмер: Санузел (пом. 4): Ст К1-1*, Ст В1-1; наличие стояка ГВС, арматуры и счётчиков — по всей квартире (К-4) О-2: обмер: Гостиная-кухня (пом. 1), Спальня (пом. 2), Детская (пом. 3); у окон	Новые перегородки заданы заказчиком в брифе положением, материалом и толщиной; конструкция (система, число слоёв, каркас, звукоизоляция, Rw) выбрана исполнителем по каталогам. (К-5)	После 1 и 2 и после получения срока у поставщика (вопроса о сроках нет); дата заказа — когда срок известен, не позднее чем за срок до начала Р-5.	срок поставки не задан (записи реестра нет)	Р-5 «черновая сантехника»: инсталляцию ставят до обшивки ГКЛВ и до гидроизоляции стены	К-4, К-5
З-7	Керамогранит и плитка: 3 поз. по артикулу и формату, 35,94 м² по раскладке пом. 1, 4, 5	О-15: обмер: Гостиная-кухня (пом. 1), Спальня (пом. 2), Детская (пом. 3), Санузел (пом. 4), Прихожая (пом. 5) О-16: обмер: Гостиная-кухня (пом. 1), Спальня (пом. 2), Детская (пом. 3), Санузел (пом. 4), Прихожая (пом. 5)		После 1 и 2 и после получения срока у поставщика (вопроса о сроках нет); дата заказа — когда срок известен, не позднее чем за срок до начала Р-10.	срок поставки не задан (записи реестра нет)	Р-10 «плитка»: калибр партии измеряют до раскладки, раскладку пересчитывают до заказа	

Допущения и предложения на листе

Основа листа: размеры помещений и положение проёмов введены заказчиком в брифе, на объекте не замерены (К-1); высота потолка 2700 мм — по брифу заказчика, не замерена (К-2); толщины стен приняты по брифу: наружные 200 мм, внутренние 150 мм — не обмерены (К-1); тип дома монолитный, перекрытие 200 мм — по брифу заказчика, документов нет (К-3); планировка (стены, проёмы, объединение кухни и гостиной, расширение санузла) — по брифу без обмера и плана БТИ (К-7); разрешённая мощность 10 кВт принята, ТУ не переданы (К-8); вентканалы приняты, в брифе не заданы (К-9); подрайон климата не задан — принят не северный (жилые от 2,5 м) (К-10).
Знак «*» — принято, не замерено и не подтверждено (замерить на объекте): К-4: Ст К1-1 — положение стояка канализации — по брифу заказчика, не замерено.
Знак «**» — предложение проектировщика, заказчиком не утверждено (согласовать с заказчиком): К-5: П-2 — положение, материал (ГКЛ) и толщина 150 мм — по брифу заказчика; конструкция (система С112, 2 слоя с каждой стороны, Rw 51 дБ — нижняя граница диапазона системы С112 (51–56 дБ)) — выбор исполнителя, автором не утверждена.
См. лист открытых вопросов (лист 6, записи К-1–К-5, К-7–К-10).

Изм.	Кол.уч	Лист	№ док.	Подп.	Дата
Разраб.		Кырлан А.С.			13.11.26
Пров.					
ГИП					
Н. контр.					
Утв.					

ГД-2026-011-АИ

Квартира 56 м²

ЖК «Северный парк», Москва

Дизайн-проект интерьера

Стадия	Лист	Листов
РП	12	119

График закупок и работ. Лист 1 из 3

М б/м

Кырлан Александр Сергеевич

выпуск 13.11.2026 № eb7810814f · стр. 12 из 139

График закупок и работ. Лист 2 из 3

ПРЕДВАРИТЕЛЬНО · не для производства работ · открыто пунктов: 13 (реестр — л. 6, 7)

Что заказывать и когда не раньше чего: относительный порядок без дат; срок поставки — из данных или «не задан» с записью реестра

Закупки: что заказывается, от чего зависит заказ и какую работу блокирует (продолжение)

№	Позиция и где	1. Замер до заказа	2. Решение, выбор изделия, паспорт	3. Условие заказа	4. Срок поставки	5. Блокирует работу	Закрывает вопросы реестра
З-8	Покрытие пола (доска) и плинтус: пом. 1, 2, 3 пом. 1, 2, 3	О-15: обмер: Гостиная-кухня (пом. 1), Спальня (пом. 2), Детская (пом. 3), Санузел (пом. 4), Прихожая (пом. 5)		После 1 и 2 и после получения срока у поставщика (вопроса о сроках нет); дата заказа — когда срок известен, не позднее чем за срок до начала Р-13.	срок поставки не задан (записи реестра нет)	Р-13 «чистовые полы»: артикул и партия — до заказа; доску привозят к чистовым полам	
З-9	Встроенная мебель по замеру цеха: Сп4, Дт2, Пр1 пом. 2, 3, 5	О-3: обмер: Вся квартира, все помещения; обход по часовой стрелке от входа (К-1)		После 1 и 2 и после получения срока у поставщика (вопроса о сроках нет); дата заказа — когда срок известен, не позднее чем за срок до начала Р-16.	срок поставки не задан (записи реестра нет) Ориентир практики (не срок поставщика): 4–8 нед. от замера	Р-16 «кухня и мебель»: цех замеряет по готовым стенам; производство 4–8 недель идёт параллельно с отделкой	К-1

Работы: порядок и что не даёт начать

№	Работа (стадия технологической последовательности)	После	Что должно быть к началу: условия и закупки	Не начинать, пока открыто в реестре
Р-1	Демонтаж покрытий, отделки стен и потолков, дверных блоков и приборов; конструкции, стены и перегородки не трогать до технического заключения (стадия 1)		до начала: запрошены документы на дом и БТИ; контрольный обмер до демонтажа (что видно) сделан	
Р-2	Контрольный обмер на голых стенах и обследование (задание — лист «Задание на контрольный обмер») (стадия 2)	Р-1	после снятия отделки: видны стояки, каналы, щиток, толщины стен; до заказа всего, что делают по размеру	
Р-3	Перегородки: разметка; кладка П-1**, П-3** (блоки, кирпич) на кладочной смеси, перемычки над проёмами; каркас и обшивка ГКЛ, фальш-стены ГКЛ (стадия 3)	Р-2	до начала: решение по нише санузла 2 принято автором; разметка по плану монтажа подписана; коробка скрытой двери — в каркас до обшивки; кладка: армирование и примыкания к несущим стенам — акт скрытых работ до штукатурки Закупки к началу: З-1 (двери скрытого монтажа)	К-1: Размеры помещений, толщины стен (наружные 200 мм, перегородки 150 мм) и положение проёмов введены заказчиком в бриф заказчика (site-brief-wizard, 01.08.2026): контрольный обмер на объекте не выполнялся, обмерного плана и плана БТИ в материалах нет; площадь по брифу 56 м², сумма помещений по чистым размерам брифа 56.37 м². К-3: Тип дома (монолитный) и толщина перекрытия 200 мм указаны заказчиком в брифе; проект дома, план БТИ и техническое заключение о несущих конструкциях не переданы. К-5: Новые перегородки заданы заказчиком в брифе положением, материалом и толщиной; конструкция (система, число слоёв, каркас, звукоизоляция, Rw) выбрана исполнителем по каталогам.
Р-4	Черновая электрика: штробы, короба, гофра, подрозетники, щит (стадия 4)	Р-2, Р-3	до начала: план электрики с высотами утверждён; штробы в стенах — только после технического заключения; мебель расставлена	К-8: Разрешённая мощность квартиры по ТУ в брифе не указана; принята 10 кВт (квартира с электроплитой, монолитный дом).
Р-5	Черновая сантехника и вентиляция: разводка, выводы, инсталляции, короба стояков (стадия 5)	Р-2, Р-3	до начала: положение стояков замерено; модели инсталляций и машины выбраны (габариты рамы, подводка); инсталляцию ставят до обшивки ГКЛВ и до гидроизоляции Закупки к началу: З-5 (стиральная машина), З-6 (сантехника)	К-4: Положение и диаметры стояков (канализации, холодной воды) указаны заказчиком в брифе, не замерены; врезки, краны и счётчики не описаны. К-5: Новые перегородки заданы заказчиком в брифе положением, материалом и толщиной; конструкция (система, число слоёв, каркас, звукоизоляция, Rw) выбрана исполнителем по каталогам.
Р-6	Коробки скрытых дверей, затем штукатурка стен и откосов (стадия 6)	Р-3, Р-4, Р-5	до начала: электрика и сантехника смонтированы, штробы заделаны; коробки скрытых дверей установлены до штукатурки (поэтому заказ дверей — раньше работы) Закупки к началу: З-2 (двери скрытого монтажа)	К-1: Размеры помещений, толщины стен (наружные 200 мм, перегородки 150 мм) и положение проёмов введены заказчиком в бриф заказчика (site-brief-wizard, 01.08.2026): контрольный обмер на объекте не выполнялся, обмерного плана и плана БТИ в материалах нет; площадь по брифу 56 м², сумма помещений по чистым размерам брифа 56.37 м².

Допущения и предложения на листе

Основа листа: размеры помещений и положение проёмов введены заказчиком в брифе, на объекте не замерены (К-1); высота потолка 2700 мм — по брифу заказчика, не замерена (К-2); толщины стен приняты по брифу: наружные 200 мм, внутренние 150 мм — не обмерены (К-1); тип дома монолитный, перекрытие 200 мм — по брифу заказчика, документов нет (К-3); планировка (стены, проёмы, объединение кухни и гостиной, расширение санузла) — по брифу без обмера и плана БТИ (К-7); разрешённая мощность 10 кВт принята, ТУ не переданы (К-8); вентканалы приняты, в брифе не заданы (К-9); подрайон климата не задан — принят не северный (жилые от 2,5 м) (К-10).

Знак «**» — предложение проектировщика, заказчиком не утверждено (согласовать с заказчиком): К-5: П-1 — положение, материал (пеноблок) и толщина 100 мм — по брифу заказчика; конструкция (кладка, армирование, штукатурка) — выбор исполнителя, автором не утверждена; кладка — не ГКЛ: каркас, листы и Rw системы не считаются (система, лист, слои, Rw — «—»); П-3 — положение, материал (кирпич) и толщина 120 мм — по брифу заказчика; конструкция (кладка, армирование, штукатурка) — выбор исполнителя, автором не утверждена; кладка — не ГКЛ: каркас, листы и Rw системы не считаются (система, лист, слои, Rw — «—»).

См. лист открытых вопросов (лист 6, записи К-1–К-3, К-5, К-7–К-10).

						ГД-2026-011-АИ		
						Квартира 56 м² ЖК «Северный парк», Москва		
Изм.	Кол.уч	Лист	№ док.	Подп.	Дата	Дизайн-проект интерьера	Стадия: РП	Лист: 13 / Листов: 119
Разраб.		Кырлан А.С.			13.11.26			
Пров.								
ГИП								
						График закупок и работ. Лист 2 из 3 М б/м	**Кырлан Александр Сергеевич**	
Н. контр.								
Утв.								

График закупок и работ. Лист 3 из 3

ПРЕДВАРИТЕЛЬНО · не для производства работ · открыто пунктов: 13 (реестр — л. 6, 7)

Что заказывать и когда не раньше чего: относительный порядок без дат; срок поставки — из данных или «не задан» с записью реестра

Работы: порядок и что не даёт начать (продолжение)

№	Работа (стадия технологической последовательности)	После	Что должно быть к началу: условия и закупки	Не начинать, пока открыто в реестре
Р-7	Стяжка пола и тёплый пол (стадия 7)	Р-6	до начала: штукатурка сделана; трубы под стяжкой приняты; нивелировка плиты выполнена	
Р-8	Гидроизоляция санузлов и тест проливом (стадия 8)	Р-7	до начала: стяжка набрала прочность и сухая по инструкции гидроизоляции; выводы стоят на проектных отметках	
Р-9	ГКЛ: короба инсталляции и стояков, ниши, потолки (стадия 9)	Р-4, Р-5	до начала: черновые сети в зоне коробов приняты; закладные под тяжёлое и карнизы стоят; светильники выбраны (вырезы)	
Р-10	Плитка и керамогранит: стены, затем пол; фартук (стадия 10)	Р-7, Р-8, Р-9	до начала: гидроизоляция принята; плитка выбрана, калибр партии измерен, раскладка пересчитана и подписана Закупки к началу: З-7 (плитка)	
Р-11	Шпаклёвка стен и потолков под окраску (стадия 11)	Р-6, Р-9, Р-10	до начала: плитка готова (грязные работы закончены); штукатурка и ГКЛ сухие	
Р-12	Окраска стен, потолков, откосов (стадия 13)	Р-11	до начала: шпаклёвка отшлифована и огрунтована; выкрасы утверждены, колеровка одной партией	
Р-13	Чистовые полы: инженерная доска (стадия 14)	Р-10, Р-12	до начала: влажность основания в норме, мокрые работы закончены; доска выбрана и привезена Закупки к началу: З-8 (доска и плинтус)	
Р-14	Полотна межкомнатных дверей, плинтусы, пороги (стадия 15)	Р-12, Р-13	до начала: чистовой пол уложен; полотна скрытых дверей — после чистовой отделки стен	
Р-15	Чистовая электрика и сантехника: механизмы, светильники, смесители, приборы (стадия 16)	Р-12, Р-14	до начала: отделка готова; механизмы, светильники и приборы выбраны и привезены	
Р-16	Кухня, встроенная и корпусная мебель, бытовая техника (стадия 17)	Р-14, Р-15	до начала: чистовая сантехника и электрика подведены к местам мебели; замер кухни снят по готовым стенам (после штукатурки или плитки, до чистового пола) Закупки к началу: З-3 (кухонный гарнитур), З-4 (техника кухни), З-9 (мебель по замеру)	К-1: Размеры помещений, толщины стен (наружные 200 мм, перегородки 150 мм) и положение проёмов введены заказчиком в бриф заказчика (site-brief-wizard, 01.08.2026): контрольный обмер на объекте не выполнялся, обмерного плана и плана БТИ в материалах нет; площадь по брифу 56 м², сумма помещений по чистым размерам брифа 56.37 м².
Р-17	Сдача: осмотр по чек-листу, дефектная ведомость, устранение замечаний (стадия 18)	Р-15, Р-16	до начала: всё смонтировано; акты скрытых работ подписаны	

Примечания

1. Порядок работ — стадии технологической последовательности из 17 позиций, присутствующих в этом проекте (по строкам ведомости объёмов); остальные стадии таблицы knowledge/remont-tehnologiya.md в проекте не встречаются. Длительности работ не печатаются: их нет ни в данных, ни в нормах для этого объекта.
2. Типовые сроки — ориентир практики, не срок поставщика: скрытые двери — короб около 10 дн., полотно под покраску до 3 нед., шпон 4–5 нед., в среднем около 30 дн. (knowledge/workers/foreman.md, п. 2.4 (profil-doors)); кухня и корпусная мебель — 4–8 недель от замера (knowledge/remont-tehnologiya.md, разд. 2; knowledge/workers/foreman.md, п. 2.4). Заказ по ориентиру не назначается: срок получают у поставщика (вопрос реестра), после чего заказ планируют «не позднее чем за срок до начала работы».
3. Условия заказа берутся из реестра открытых вопросов и задания на контрольный обмер: позиция заказывается, когда закрыты замер (графа 1) и решение (графа 2). Закрывать их может только факт или решение автора с подписью; снять строку с листа можно только закрыв запись реестра.
4. Заказ по размеру до контрольного обмера не делают: двери, кухня и встроенная мебель зависят от обмера (К-11, К-13); скрытые двери, кроме того, зависят от решения по нише санузла 2 (проём Д-5 в перегородке П-1**).
5. Номера листов — по ведомости рабочих чертежей комплекта (лист «Общие данные»).

Допущения и предложения на листе

Основа листа: размеры помещений и положение проёмов введены заказчиком в брифе, на объекте не замерены (К-1); высота потолка 2700 мм — по брифу заказчика, не замерена (К-2); толщины стен приняты по брифу: наружные 200 мм, внутренние 150 мм — не обмерены (К-1); тип дома монолитный, перекрытие 200 мм — по брифу заказчика, документов нет (К-3); планировка (стены, проёмы, объединение кухни и гостиной, расширение санузла) — по брифу без обмера и плана БТИ (К-7); разрешённая мощность 10 кВт принята, ТУ не переданы (К-8); вентканалы приняты, в брифе не заданы (К-9); подрайон климата не задан — принят не северный (жилые от 2,5 м) (К-10).

Знак «**» — предложение проектировщика, заказчиком не утверждено (согласовать с заказчиком): К-5: П-1 — положение, материал (пеноблок) и толщина 100 мм — по брифу заказчика; конструкция (кладка, армирование, штукатурка) — выбор исполнителя, автором не утверждена; кладка — не ГКЛ: каркас, листы и Rw системы не считаются (система, лист, слои, Rw — «—»).

См. лист открытых вопросов (лист 6, записи К-1–К-3, К-5, К-7–К-10).

Изм.	Кол.уч	Лист	№ док.	Подп.	Дата
Разраб.		Кырлан А.С.			13.11.26
Пров.					
ГИП					
Н. контр.					
Утв.					

ГД-2026-011-АИ

Квартира 56 м²

ЖК «Северный парк», Москва

Дизайн-проект интерьера

Стадия	Лист	Листов
РП	14	119

График закупок и работ. Лист 3 из 3

М б/м

Кырлан Александр Сергеевич


выпуск 13.11.2026 № eb7810814f · стр. 14 из 139

Календарный график работ и закупок

ПРЕДВАРИТЕЛЬНО · не для производства работ · открыто пунктов: 13 (реестр — л. 6, 7)

Недели, зависимости, техпаузы и даты заказа длинных позиций · длительности — ориентир по таблице типовых сроков, не обещание бригады

№	Работа	Нед.	После
Р-1	**демонтаж**	1	
Р-2	**контрольный обмер**	0,5	Р-1
Р-3	**перегородки**	0,75	Р-2
Р-4	**черновая электрика**	1,25	Р-3, Р-2
Р-5	черновая сантехника	1	Р-3, Р-2
Р-6	**штукатурка**	2	Р-4, Р-5, Р-3
Р-7	**стяжка**	0,75	Р-6
Р-8	**гидроизоляция**	0,5	Р-7
Р-9	ГКЛ	1,25	Р-4, Р-5
Р-10	**плитка**	2,75	Р-8, Р-9, Р-7
Р-11	**шпаклёвка**	2,25	Р-10, Р-9, Р-6
Р-12	**окраска**	1,75	Р-11
Р-13	**чистовые полы**	1	Р-12, Р-10
Р-14	**двери и плинтусы**	0,75	Р-13, Р-12
Р-15	**чистовая электрика и сантехника**	0,75	Р-14, Р-12
Р-16	**кухня и мебель**	0,75	Р-15, Р-14
Р-17	**сдача**	0,5	Р-16, Р-15
Закупки: заказать не позднее — «◆»; от заказа до поставки — штриховая полоса; срок поставки — только из данных или «ориентир практики»			
З-1	Двери скрытого монтажа с коробом под покраску в новой перегородке П-2**: Д-4 — 1 шт.	4,25	для Р-3
З-2	Двери скрытого монтажа с коробом под покраску в существующих проёмах: Д-2, Д-3, Д-5 — 3 шт	4,25	для Р-6
З-3	Кухонный гарнитур по проекту кухни: модули Кх1, Кх2, Кх3, Кх4, Кх5, Кх6, Кх7, Кх8, Кх9, Кх	6	для Р-16
З-4	Встраиваемая техника кухни: Кх1 холодильник, Кх6 посудомоечная машина, Кх8 вытяжка		для Р-16
З-5	Стиральная машина: Сн4 (вертикальная загрузка 400 × 600 мм — условие закупки)		для Р-5
З-6	Сантехнические приборы и инсталляции: П1, Сн1, Сн2, Сн3		для Р-5
З-7	Керамогранит и плитка: 3 поз. по артикулу и формату, 35,94 м² по раскладке		для Р-10
З-8	Покрытие пола (доска) и плинтус: пом. 1, 2, 3		для Р-13
З-9	Встроенная мебель по замеру цеха: Сп4, Дт2, Пр1	6	для Р-16

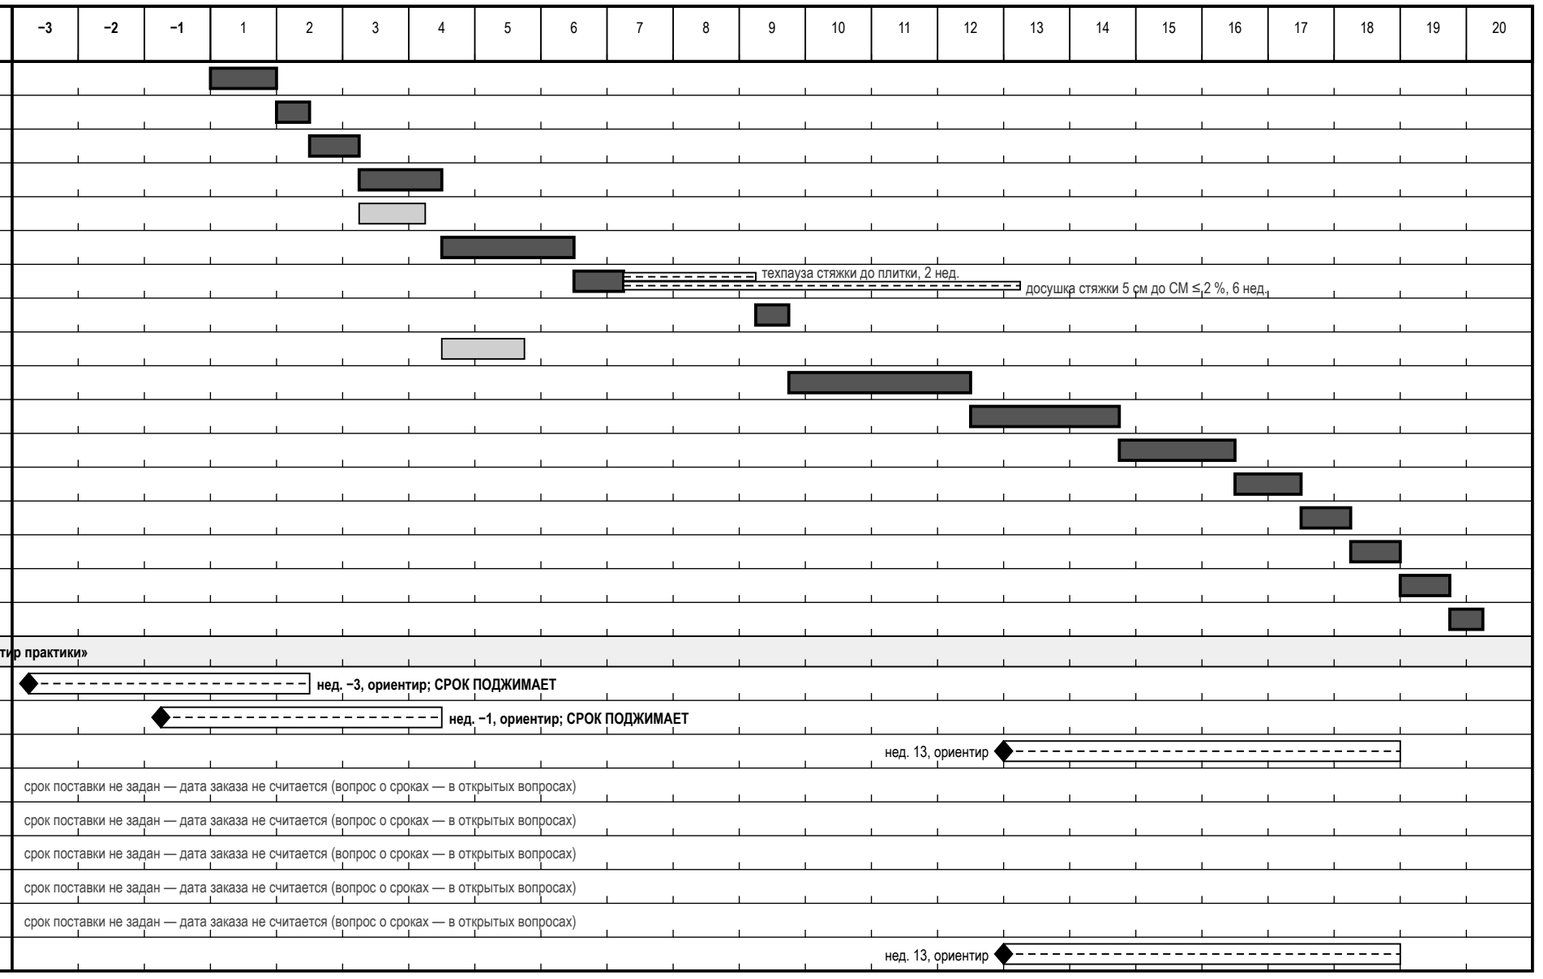

Итого: ≈ 19,25 нед. · жирная линия и тёмная полоса — критический путь

Примечания

1. Длительности этапов — типовые сроки по площади 56,37 м² (таблица «Свод для графика»: недели по этапам для 45, 80 и 120 м², середина вилки, линейная интерполяция); это ориентир, а не норма и не обещание бригады. Контрольный обмер — ориентир 0,5 нед. (в таблице нет).
2. Зависимости «после» — из графика закупок и работ (лист «График закупок и работ»); каждая работа начинается после конца предшественников. Техпаузы стоят отдельными полосами, а не спрятаны в длительности: стяжка → плитка — не менее 2 нед.; стяжка → чистовой пол — досушка стяжки 5 см до СМ ≤ 2 % — 6 нед. (ориентир «1 нед. на 1 см до 4 см, 5 см — 6 нед., 6 см — 8 нед.»; решает замер).
3. График последовательный и поэтому консервативный: в жизни шпаклёвка, плитка и досушка стяжки идут частично параллельно (таблица типовых сроков для 56,37 м²: 13–17 нед.). Совмещения — решение прораба после обмера.
4. Закупки: «заказать не позднее» = начало работы, которой нужна позиция, минус срок поставки. Срок поставки — из данных проекта (срок поставки позиции, срок изготовления обоев в отделке); если его нет, в графике стоит типовой диапазон практики с пометкой «ориентир» — это не срок поставщика, его надо получить до заказа. Кухню и встроенную мебель заказывают после замера по готовым стенам (после штукатурки). Позиции без срока дат заказа не имеют.
5. «Срок поджимает»: самая поздняя дата заказа раньше, чем позицию можно заказать (до замера или обмера): сдвиньте начало работ, ищите изделие с меньшим сроком или заказывайте по предварительному размеру — решение прораба и заказчика.

Допущения и предложения на листе

Основа листа: размеры помещений и положение проёмов введены заказчиком в брифе, на объекте не замерены (К-1); высота потолка 2700 мм — по брифу заказчика, не замерена (К-2); толщины стен приняты по брифу: наружные 200 мм, внутренние 150 мм — не обмерены (К-1); тип дома монолитный, перекрытие 200 мм — по брифу заказчика, документов нет (К-3); планировка (стены, проёмы, объединение кухни и гостиной, расширение санузла) — по брифу без обмера и плана БТИ (К-7); разрешённая мощность 10 кВт принята, ТУ не переданы (К-8); вентканалы приняты, в брифе не заданы (К-9); подрайон климата не задан — принят не северный (жилые от 2,5 м) (К-10).
Знак «**» — предложение проектировщика, заказчиком не утверждено (согласовать с заказчиком): К-5: П-2 — положение, материал (ГКЛ) и толщина 150 мм — по брифу заказчика; конструкция (система С112, 2 слоя с каждой стороны, Rw 51 дБ — нижняя граница диапазона системы С112 (51–56 дБ)) — выбор исполнителя, автором не утверждена.
См. лист открытых вопросов (лист 6, записи К-1–К-3, К-5, К-7–К-10).

Изм.	Кол.уч	Лист	№ док.	Подп.	Дата
Разраб.		Кырлан А.С.			13.11.26
Пров.					
ГИП					
Н. контр.					
Утв.					

ГД-2026-011-АИ

Квартира 56 м²

ЖК «Северный парк», Москва

Дизайн-проект интерьера

Стадия	Лист	Листов
РП	15	119

Календарный график работ и закупок

М б/м

Кырлан Александр Сергеевич

выпуск 13.11.2026 · eb7810814f · стр. 15 из 139

Чек-лист приёмки по этапам. Лист 1 из 4

По этапам Р-1…Р-N: что проверить, чем, какой допуск и какой акт подписать до закрытия работы

Приёмка по этапам: контрольные точки, допуски и акты скрытых работ

Этап	Контрольная точка (дальше не пускают без подписи)	Что проверяют	Чем	Допуск	Основание	Подпись	Акт скрытых работ / документ
Р-1	Демонтаж До начала демонтажа: запрошены документы на дом и БТИ	Что снимается и что не трогается: покрытия, отделка, дверные блоки; несущие стены и перегородки — без изменений	осмотр по плану демонтажа	снятое — только по плану; несущее не затрагивать	практика		Фото помещений до и после демонтажа; перечень снятого в журнале работ.
Р-2	Контрольный обмер Контрольный обмер на голых стенах сделан до заказа всего, что делают по размеру	Размеры помещений и проёмов, диагонали, положение стояков, щитка, каналов, толщины стен	рулетка, лазерный дальномер, уровень	допуск задаёт проект; расхождение с планом — в перечень открытых вопросов до заказа	практика		Протокол контрольного обмера с эскизом; расхождения занесены в открытые вопросы.
Р-3	Перегородки Перегородки: разметка против плана монтажа подписана до обшивки	Шаг саморезов: потолок 150 мм; стена 200 мм (лист вертикально) или 300 мм (горизонтально)	рулетка	150 / 200 / 300 мм	практика (СП 163.1325800.2014)		Акт скрытых работ: каркас ГКЛ, закладные под тяжёлое, звукоизоляция в перегородках — до обшивки (фото закладных с привязками); армирование и примыкание к несущим.
		Отступ самореза от кромки и угла листа; расстояние между саморезами на стыке листов	рулетка	5–10 мм от кромки; не менее 15 мм на стыке	практика (СП 163.1325800.2014)		
		Заделка стыков: лента и не менее 2 слоёв шпаклёвки; шляпки утоплены вровень, без прорыва картона	визуально, на просвет	без трещин после высыхания	практика		
		Прогиб каркаса: нет люфта между листом и профилем	простукивание, нажатие рукой	точной цифры нет — сверить перед актом	практика		
Р-4	Черновая электрика Черновая электрика: трассы, высоты подрозетников, замер изоляции подписаны до заделки	Сопротивление изоляции проводки (цепи до 1000 В)	мегаомметр	не менее 0,5 МОм	норматив (ПУЭ, гл. 1.8)		Акт скрытых работ на трассы проводки и слаботочные линии до закрытия штукатуркой и ГКЛ; исполнительная схема трасс с привязками; заземление и уравнивание потенциалов в санузле протокол и фото.
		Целостность и маркировка: PE жёлто-зелёный, N — синий, L — прочие цвета	визуально, прозвонка	каждый проводник промаркирован	практика		
		Высоты подрозетников и привязки — по плану розеток и выключателей	рулетка, уровень	по проекту; от чистого пола	практика		
Р-5	Черновая сантехника Черновая сантехника: опрессовка, отметки выводов, инсталляции подписаны до зашивки	Опрессовка водоснабжения: рабочее давление до 0,6 МПа — испытание 0,9 МПа; выше 0,6 МПа — по расчёту	опрессовочный насос, манометр	выдержка 10 мин (поквартирная); падение: пластик не более 0,06 МПа за 30 мин, сталь не более 0,05 МПа за 10 мин	практика (СП 73.13330)		Акт опрессовки (давление, время, результат); акт скрытых работ на трассы в стенах, полу и коробах; инсталляции, скрытые смесители, трапы — фото с рулеткой и отметками.
		Уклон канализации Ø40–50	уровень, построитель плоскостей	не менее 20 мм на 1 м	норматив (СП 30.13330)		
		Протечки в соединениях, сифоны, смесители, гибкая подводка	осмотр под давлением, салфетка на стыках	нет капель и влажных следов в контрольное время	практика		

Допущения и предложения на листе

Основа листа: размеры помещений и положение проёмов введены заказчиком в брифе, на объекте не замерены (К-1); высота потолка 2700 мм — по брифу заказчика, не замерена (К-2); толщины стен приняты по брифу: наружные 200 мм, внутренние 150 мм — не обмерены (К-1); тип дома монолитный, перекрытие 200 мм — по брифу заказчика, документов нет (К-3); планировка (стены, проёмы, объединение кухни и гостиной, расширение санузла) — по брифу без обмера и плана БТИ (К-7); разрешённая мощность 10 кВт принята, ТУ не переданы (К-8); вентканалы приняты, в брифе не заданы (К-9); подрайон климата не задан — принят не северный (жилые от 2,5 м) (К-10).

См. лист открытых вопросов (лист 6, записи К-1–К-3, К-7–К-10).

Изм.	Кол.уч	Лист	№ док.	Подп.	Дата
Разраб.		Кырлан А.С.			13.11.26
Пров.					
ГИП					
Н. контр.					
Утв.					

ГД-2026-011-АИ

Квартира 56 м²

ЖК «Северный парк», Москва

Дизайн-проект интерьера

Стадия	Лист	Листов
РП	16	119

Чек-лист приёмки по этапам. Лист 1 из 4

М б/м

Кырлан Александр Сергеевич

выпуск 13.11.2026 № eb7810814f · стр. 16 из 139

Чек-лист приёмки по этапам. Лист 2 из 4

По этапам Р-1…Р-N: что проверить, чем, какой допуск и какой акт подписать до закрытия работы

Приёмка по этапам: контрольные точки, допуски и акты скрытых работ (продолжение)

Этап	Контрольная точка (дальше не пускают без подписи)	Что проверяют	Чем	Допуск	Основание	Подпись	Акт скрытых работ / документ
		Отметки выводов и положение инсталляций до зашивки и гидроизоляции	рулетка в кадре, фото	по листу выводов	практика		
Р-6	Штукатурка Маяки стен проверены до штукатурки; коробки скрытых дверей стоят до штукатурки	Отклонение от вертикали (простая / улучшенная / высококачественная штукатурка)	отвес, лазерный уровень	3 / 2 / 1 мм на 1 м; не более 15 / 10 / 5 мм на высоту	практика (СП 71.13330.2017)		Фото коробок скрытых дверей с отметкой чистого пола — до штукатурки; класс штукатурки (простая / улучшенная / высококачественная) назван в договоре.
		Отклонение от горизонтали	уровень, правило	3 / 2 / 1 мм на 1 м; не более 15 / 10 / 5 мм на длину	практика (СП 71.13330.2017)		
		Неровности (плоскостность)	правило 2 м и щуп	до 5 / 3 / 2 мм на 1 м; не более 3 / 2 / 2 неровностей на 4 м²	практика (СП 71.13330.2017)		
		Влажность основания перед шпаклёвкой и отделкой	влагомер	верхние 20–30 мм — не более 5 % по массе	норматив (СП 71, табл. 7.2)		
Р-7	Стяжка Стяжка: подготовка, после заливки ровность, затем замер СМ перед чистовым полом	Ровность: просвет под рейкой 2 м	рейка 2 м, клиновой щуп	под паркет, ламинат — 2 мм; под гидроизоляцию до 4 мм; прочие покрытия — до 6 мм (цифры расходятся между источниками — сверить перед актом)	практика (СП 29.13330)		Акт скрытых работ на стяжку (толщина, армирование) до чистового пола; протокол ровности и протокол СМ-влажности; звукоизоляция и демпферная лента под стяжкой — фото и паспорт; контуры тёплого пола до заливки — схема укладки и замер сопротивления.
		Отклонение от горизонтали по помещению	уровень, нивелир	не более 0,2 % длины помещения	практика (СП 29.13330)		
		Число точек измерения	рейка	не менее 3 на 30 м² или 1 на небольшое помещение	практика		
		Отслоения и пустоты	простукивание молотком или киянкой	глухой звук — зона вскрывается и переделывается	практика		
		Влажность перед укладкой доски: цементная стяжка	влагомер; СМ-замер	ЦПС не более 2,0 % СМ (с тёплым полом не более 1,8 %); влагомер для плитки — не более 5 %	практика (СП 71; рекомендации производителей)		
Р-8	Гидроизоляция Гидроизоляция: пролив 24 ч подпись до плитки	Заведение на стены не ниже 200 мм от чистого пола; за ванной — 300 мм выше борта; в душе без поддона — на высоту лейки	рулетка	не менее 200 мм	норматив (СП 71.13330.2017, п. 8.6.5); остальное — практика		Акт теста проливом, фото узлов и высоты заведения на стены — до плитки.
		Тест проливом: слой воды 10–30 мм, контроль уровня и потолка соседа снизу	линейка, визуально	24 ч (минимум 12 ч); падения уровня и протечки нет	практика		
		Два слоя обмазки с межслойной сушкой, лента в углах и манжеты на выводах	визуально	по инструкции производителя	практика		
Р-9	ГКЛ Короба, ниши и потолки: черновые сети в зоне коробов приняты до обшивки	Шаг саморезов, отступ от кромки, заделка стыков (как у перегородок)	рулетка, визуально	потолок 150 мм; кромка 5–10 мм; стык — лента и 2 слоя шпаклёвки	практика (СП 163.1325800.2014)		Акт скрытых работ: каркас ГКЛ, закладные, звукоизоляция — фото до обшивки; воздуховоды в коробах и за потолком — фото и схема.

Допущения и предложения на листе

Основа листа: размеры помещений и положение проёмов введены заказчиком в брифе, на объекте не замерены (К-1); высота потолка 2700 мм — по брифу заказчика, не замерена (К-2); толщины стен приняты по брифу: наружные 200 мм, внутренние 150 мм — не обмерены (К-1); тип дома монолитный, перекрытие 200 мм — по брифу заказчика, документов нет (К-3); планировка (стены, проёмы, объединение кухни и гостиной, расширение санузла) — по брифу без обмера и плана БТИ (К-7); разрешённая мощность 10 кВт принята, ТУ не переданы (К-8); вентканалы приняты, в брифе не заданы (К-9); подрайон климата не задан — принят не северный (жилые от 2,5 м) (К-10).

См. лист открытых вопросов (лист 6, записи К-1–К-3, К-7–К-10).

Изм.	Кол.уч	Лист	№ док.	Подп.	Дата
Разраб.		Кырлан А.С.			13.11.26
Пров.					
ГИП					
Н. контр.					
Утв.					

ГД-2026-011-АИ

Квартира 56 м²

ЖК «Северный парк», Москва

Дизайн-проект интерьера

Стадия	Лист	Листов
РП	17	119

Чек-лист приёмки по этапам. Лист 2 из 4

М б/м

Кырлан Александр Сергеевич

выпуск 13.11.2026 № eb7810814f · стр. 17 из 139

Чек-лист приёмки по этапам. Лист 3 из 4

По этапам Р-1…Р-N: что проверить, чем, какой допуск и какой акт подписать до закрытия работы

Приёмка по этапам: контрольные точки, допуски и акты скрытых работ (продолжение)

Этап	Контрольная точка (дальше не пускают без подписи)	Что проверяют	Чем	Допуск	Основание	Подпись	Акт скрытых работ / документ
		Закладные под тяжёлое, карнизы, подвесные светильники на месте до обшивки	фото с привязками	по плану потолков и узлам	практика		
		Ревизионные люки: доступ к арматуре и ревизиям сохранён	осмотр	по листу ВК	практика		
Р-10	Плитка Раскладка плитки: первая плита и первый ряд проверены по развёртке; плитка выбрана, калибр партии измерен	Уступы между смежными плитками	линейка, на просвет	не более 1 мм	норматив (СП 71.13330.2017)		Раскладка подписана до начала плитки; протокол первого ряда; акт теста проливом приложен (этап гидроизоляции).
		Ширина шва и его прямолинейность	линейка, калибр	до 6 мм ручная укладка; фактическая по проекту ±0,5 мм	практика		
		Отклонение рядов от вертикали и горизонтали	уровень, правило, отвес	1,5 мм на 1 м длины	практика		
		Ровность облицовки	правило 2 м и щуп	не более 2–4 мм (цифра расходится по источникам)	практика		
		Пустоты под плиткой	простукивание всей площади	до 10 % площади допустимо; свыше 25 % под одной плиткой — брак	практика		
Р-11	Шпаклёвка Шпаклёвка Q3/Q4: проверка боковым светом до окраски	Класс основания под окраску: Q3 — сплошное финишное шпаклевание; Q4 — под направленный свет	переносной прожектор у поверхности под острым углом	Q3: царапины от абразива до 0,5 мм; Q4 — без видимых царапин и теней; неровность на 2 м: Q3 — 1 мм, Q4 — 0,5 мм	практика (Q-классы — не норматив СП, а согласованный критерий)		Класс (Q3 или Q4) назван в договоре; грунтование и армирование стыков перед шпаклёвкой — запись в журнале.
Р-12	Окраска Выкрасы утверждены, колеровка одной партией	Окраска без полос, подтёков, пропусков; цвет — по колерной карте	боковой свет, образец выкраса	без видимых дефектов при боковом свете	практика		Утверждённые выкрасы; остаток колеровки одной партии — для подкраски.
		Основание сухое, огрунтованное; защита от прямого солнца при высыхании	осмотр	по ТУ краски	норматив (СП 71.13330.2017, п. 7.5.2)		
Р-13	Чистовые полы Чистовые полы: влажность, ровность, уступы, зазоры — до укладки доски; мокрые работы закончены	Деформационный зазор у стен и порогов (доска, ламинат)	линейка, клинья при укладке	8–15 мм (чаще 10 мм); у ламината 5–10 мм по СП 71	практика (требования производителей); норматив (СП 71, п. 8.10.14)		Протокол СМ-влажности стяжки до укладки; паспорт и партия доски.
		Перепад основания под покрытие	правило 2 м и щуп	не более 2 мм на 2 м	практика		
		Зазоры и перепады между досками; скрип; видимый зазор в замке — брак	щуп, рука, шаг	«ступеньки» нет	практика		
		Влажность помещения при укладке и после	гигрометр	не более 60 %, без сквозняков	норматив (СП 71, п. 8.1.7)		

Допущения и предложения на листе

Основа листа: размеры помещений и положение проёмов введены заказчиком в брифе, на объекте не замерены (К-1); высота потолка 2700 мм — по брифу заказчика, не замерена (К-2); толщины стен приняты по брифу: наружные 200 мм, внутренние 150 мм — не обмерены (К-1); тип дома монолитный, перекрытие 200 мм — по брифу заказчика, документов нет (К-3); планировка (стены, проёмы, объединение кухни и гостиной, расширение санузла) — по брифу без обмера и плана БТИ (К-7); разрешённая мощность 10 кВт принята, ТУ не переданы (К-8); вентканалы приняты, в брифе не заданы (К-9); подрайон климата не задан — принят не северный (жилые от 2,5 м) (К-10).

См. лист открытых вопросов (лист 6, записи К-1–К-3, К-7–К-10).

Изм.	Кол.уч	Лист	№ док.	Подп.	Дата
Разраб.		Кырлан А.С.			13.11.26
Пров.					
ГИП					
Н. контр.					
Утв.					

ГД-2026-011-АИ

Квартира 56 м²

ЖК «Северный парк», Москва

Дизайн-проект интерьера

Стадия	Лист	Листов
РП	18	119

Чек-лист приёмки по этапам. Лист 3 из 4

М б/м

Кырлан Александр Сергеевич

Чек-лист приёмки по этапам. Лист 4 из 4

По этапам Р-1…Р-N: что проверить, чем, какой допуск и какой акт подписать до закрытия работы

Приёмка по этапам: контрольные точки, допуски и акты скрытых работ (продолжение)

Этап	Контрольная точка (дальше не пускают без подписи)	Что проверяют	Чем	Допуск	Основание	Подпись	Акт скрытых работ / документ
Р-14	Двери и плинтусы Полотна и плинтусы — после чистового пола; скрытые полотна после чистовой отделки стен	Отклонение коробки от вертикали	отвес, уровень	1,5 мм на 1 м, не более 3 мм на коробку	практика (ТР 105-00, пересказ)		Коробки скрытых дверей приняты до штукатурки (этап штукатурки); паспорт на полотна.
		Зазор между полотном и коробкой по периметру	щуп	2–4 мм по бокам и верху (единого норматива нет)	практика		
		Открывание и закрывание: без перекоса, плавный ход петель и доводчика	визуально, от руки	без задевания коробки и пола	практика		
Р-15	Чистовая электрика и сантехника Чистовая электрика и сантехника: протокол электролаборатории и проверка УЗО до подписи акта	УЗО: кнопка «Тест»; время отключения; ток отключения	кнопка на аппарате; прибор проверки УЗО (не мультиметр)	отключает; не более 0,3 с; 50–100 % от IΔn	практика измерений		Протокол измерений аккредитованной электролаборатории (изоляция по группам, УЗО, PE, фаза-ноль); исполнительная схема щита; акт опрессовки приложен (этап ВК).
		Сопротивление изоляции готовых линий; петля фаза-ноль для срабатывания автоматов	мегаомметр; прибор петли фаза-ноль	изоляция не менее 0,5 МОм; петля — по проекту	норматив (ПУЭ, гл. 1.8) / по проекту		
		Смесители, сифоны, гибкая подводка: пробный пуск воды	визуально под нагрузкой	нет подтёков в контрольное время	практика		
Р-16	Кухня и мебель Кухня и мебель: замер кухни снят по готовым стенам; чистовая электрика и сантехника подведены	Привязка выводов и розеток к модулям кухни; вытяжка, вентиляция	рулетка, сверка с листом кухни	по проекту кухни	практика		Акт передачи кухни; паспорта техники и гарантийные талоны.
		Тяга вентиляции у решёток	лист бумаги у решётки	бумага притягивается; при сомнениях — замер анемометром	практика		
Р-17	Сдача Финальная приёмка по таблицам СП 71: дефектная ведомость и акт	Стены, потолки, полы, плитка, двери, окна осмотр по чек-листу этапов выше	правило 2 м, уровень, щуп, боковой свет, влагомер	по таблицам выше	практика		Дефектная ведомость и акт приёмки; гарантия: по умолчанию претензии по качеству работ — 2 года, в договоре прописывается отдельно.
		Полный пакет документов: акты скрытых работ, протокол электролаборатории, акт опрессовки, исполнительные схемы, гарантийные обязательства	комплектность	пакет собран до подписи акта	практика		

Примечания

1. Метка основания: «норматив» — цифра подтверждена текстом СП, ГОСТ или ПУЭ; «практика» — отраслевая конвенция или один источник: к спору не годится без сверки первоисточника (СП 71.13330.2017, СП 29.13330, СП 163.1325800.2014, ПУЭ гл. 1.8, СП 73.13330, СП 30.13330).
2. Класс штукатурки (простая / улучшенная / высококачественная) и класс основания под окраску (Q3 или Q4) называются в договоре подряда: допуск выбирается по ним. Q-классы — не норматив, а согласованный сторонами критерий.
3. Акт скрытых работ подписывают до того, как работа закрыта следующим слоем (штукатуркой, плиткой, стяжкой, обшивкой): постфактум он слабее — осматривать нечего. Подписывают заказчик (или технадзор), подрядчик; при перепланировке — автор проекта. Каждую зону снимают до закрытия с рулеткой в кадре и привязкой к стене.
4. По умолчанию, если срок не прописан в договоре, претензии по качеству работ можно предъявить в течение 2 лет со дня приёмки; в договоре гарантийный срок и сроки на скрытые работы рекомендуется назвать явно.

Допущения и предложения на листе

Основа листа: размеры помещений и положение проёмов введены заказчиком в брифе, на объекте не замерены (К-1); высота потолка 2700 мм — по брифу заказчика, не замерена (К-2); толщины стен приняты по брифу: наружные 200 мм, внутренние 150 мм — не обмерены (К-1); тип дома монолитный, перекрытие 200 мм — по брифу заказчика, документов нет (К-3); планировка (стены, проёмы, объединение кухни и гостиной, расширение санузла) — по брифу без обмера и плана БТИ (К-7); разрешённая мощность 10 кВт принята, ТУ не переданы (К-8); вентканалы приняты, в брифе не заданы (К-9); подрайон климата не задан — принят не северный (жилые от 2,5 м) (К-10).

См. лист открытых вопросов (лист 6, записи К-1–К-3, К-7–К-10).

Изм.	Кол.уч	Лист	№ док.	Подп.	Дата
Разраб.		Кырлан А.С.			13.11.26
Пров.					
ГИП					
Н. контр.					
Утв.					

ГД-2026-011-АИ

Квартира 56 м²

ЖК «Северный парк», Москва

Дизайн-проект интерьера

Стадия	Лист	Листов
РП	19	119

Чек-лист приёмки по этапам. Лист 4 из 4

М б/м

Кырлан Александр Сергеевич

Лист → мастер

Мастер → листы альбома и документы, которые ему нужны

Какому мастеру какие листы (номера — как в штампе)

Мастер	Что делает по альбому	Листы	Кроме чертежей — документы	Листов
Замерщик и прораб (до начала работ)	Контрольный обмер на голых стенах, сверка размеров и диагоналей, ответы на открытые вопросы до заказа	2–11, 21	Задание на контрольный обмер; лист открытых вопросов	11
Гипсокартонщик и монтажник перегородок	Демонтаж и возведение перегородок, каркас, короба инсталляции, ниши, потолки; закладные под навесное	22, 52–56, 77, 79	Ведомость материалов каркаса; акт скрытых работ на каркас	8
Электрик	Группы щита, подрозетники и высоты, трассы, свет, управление светом, слаботочка, тёплый пол	32–40, 51, 83–101	Таблица нагрузок; ведомость изделий; протокол электролаборатории	29
Сантехник	Выводы воды и канализации, разводка, аксонометрии, инсталляции, короба стояков	43–50, 83–101	Спецификация ВК; акт опрессовки; акт пролива	27
Монтажник вентиляции, отопления и кондиционеров	Вентиляция, радиаторы и тёплые полы, кондиционеры: места, размеры, трассы и дренаж	41–42	Акт опрессовки азотом (кондиционеры); фото воздуховодов до закрытия	2
Штукатур, шпаклёвщик, маляр, паркетчик	Основание стен, окраска и обои по колерной карте, полы и пороги, плинтус, узлы стыков	60–63, 83–103	Колерная карта и выкрасы; спецификация отделочных материалов	25
Плиточник	Раскладка и подрезка плитки стен, пола и фартука, гидроизоляция, швы, выводы в плитке	48–49, 57–59, 83–103	Ведомость плитки; акт теста проливом	26
Монтажник дверей и окон	Заполнение проёмов: размеры коробок, открывание, пороги, скрытые двери	25	Ведомость проёмов; паспорта на полотна	1
Мебельщик, кухонный монтажник	Кухня и мебель на заказ: габариты, членение, фурнитура, связка с электрикой и сантехникой	27–31, 70–81	Ведомость изделий; замер кухни по готовым стенам	17
Заказчик и комплектатор	Что и когда покупать, сколько с запасом, во что это обойдётся; свет, декор и текстиль; визуализации как должно получиться	1, 12–15, 51, 64–65, 68–69, 104–119	Список покупок; смета; календарный график	26
Прораб и технадзор (приёмка)	Приёмка этапов, акты скрытых работ, дефектная ведомость	15–20	Чек-лист приёмки по этапам; календарный график	6

Примечания

1. Номера листов — как в основной надписи: основные подряд (1, 2, 3…), «Д» — детализация мебели, «С» — ведомости, спецификации, узлы и сметы, «П» — приложение единого комплекта. «12–18» — все листы с 12 по 18.
2. Лист может быть у нескольких мастеров: развёртка стены нужна электрику (высоты точек), сантехнику (выводы), отделочнику (материалы) и плиточнику (раскладка). Общие листы (обмер, список листов, перечень вопросов) прораб раздаёт всем.
3. Мастер работает по чертежам и берёт в руки то, что назначено ему здесь; закупки, смету и график ведёт заказчик с прорабом. Лист, которого нет в таблице ни у одного мастера, — вопрос прорабу: чей он.

Допущения и предложения на листе

Основа листа: размеры помещений и положение проёмов введены заказчиком в брифе, на объекте не замерены (К-1); высота потолка 2700 мм — по брифу заказчика, не замерена (К-2); толщины стен приняты по брифу: наружные 200 мм, внутренние 150 мм — не обмерены (К-1); тип дома монолитный, перекрытие 200 мм — по брифу заказчика, документов нет (К-3); планировка (стены, проёмы, объединение кухни и гостиной, расширение санузла) — по брифу без обмера и плана БТИ (К-7); разрешённая мощность 10 кВт принята, ТУ не переданы (К-8); вентканалы приняты, в брифе не заданы (К-9); подрайон климата не задан — принят не северный (жилые от 2,5 м) (К-10).

См. лист открытых вопросов (лист 6, записи К-1–К-3, К-7–К-10).

Изм.	Кол.уч	Лист	№ док.	Подп.	Дата				
Разраб.		Кырлан А.С.			13.11.26	ГД-2026-011-АИ			
Пров.						Квартира 56 м² ЖК «Северный парк», Москва			
ГИП						Дизайн-проект интерьера	Стадия	Лист	Листов
							РП	20	119
Н. контр.						Лист → мастер М б/м	Кырлан Александр Сергеевич		
Утв.									

выпуск 13.11.2026 № eb78108814f · стр. 20 из 139

01

Архитектурные решения


Кырлан Александр Сергеевич

выпуск 13.11.2026 SI eb7810814f · стр. 21 из 139

Обмерный план

Существующее положение · размеры в мм · отметки от чистого пола

ПРЕДВАРИТЕЛЬНО · не для производства работ · открыто пунктов: 13 (реестр — л. 6, 7)

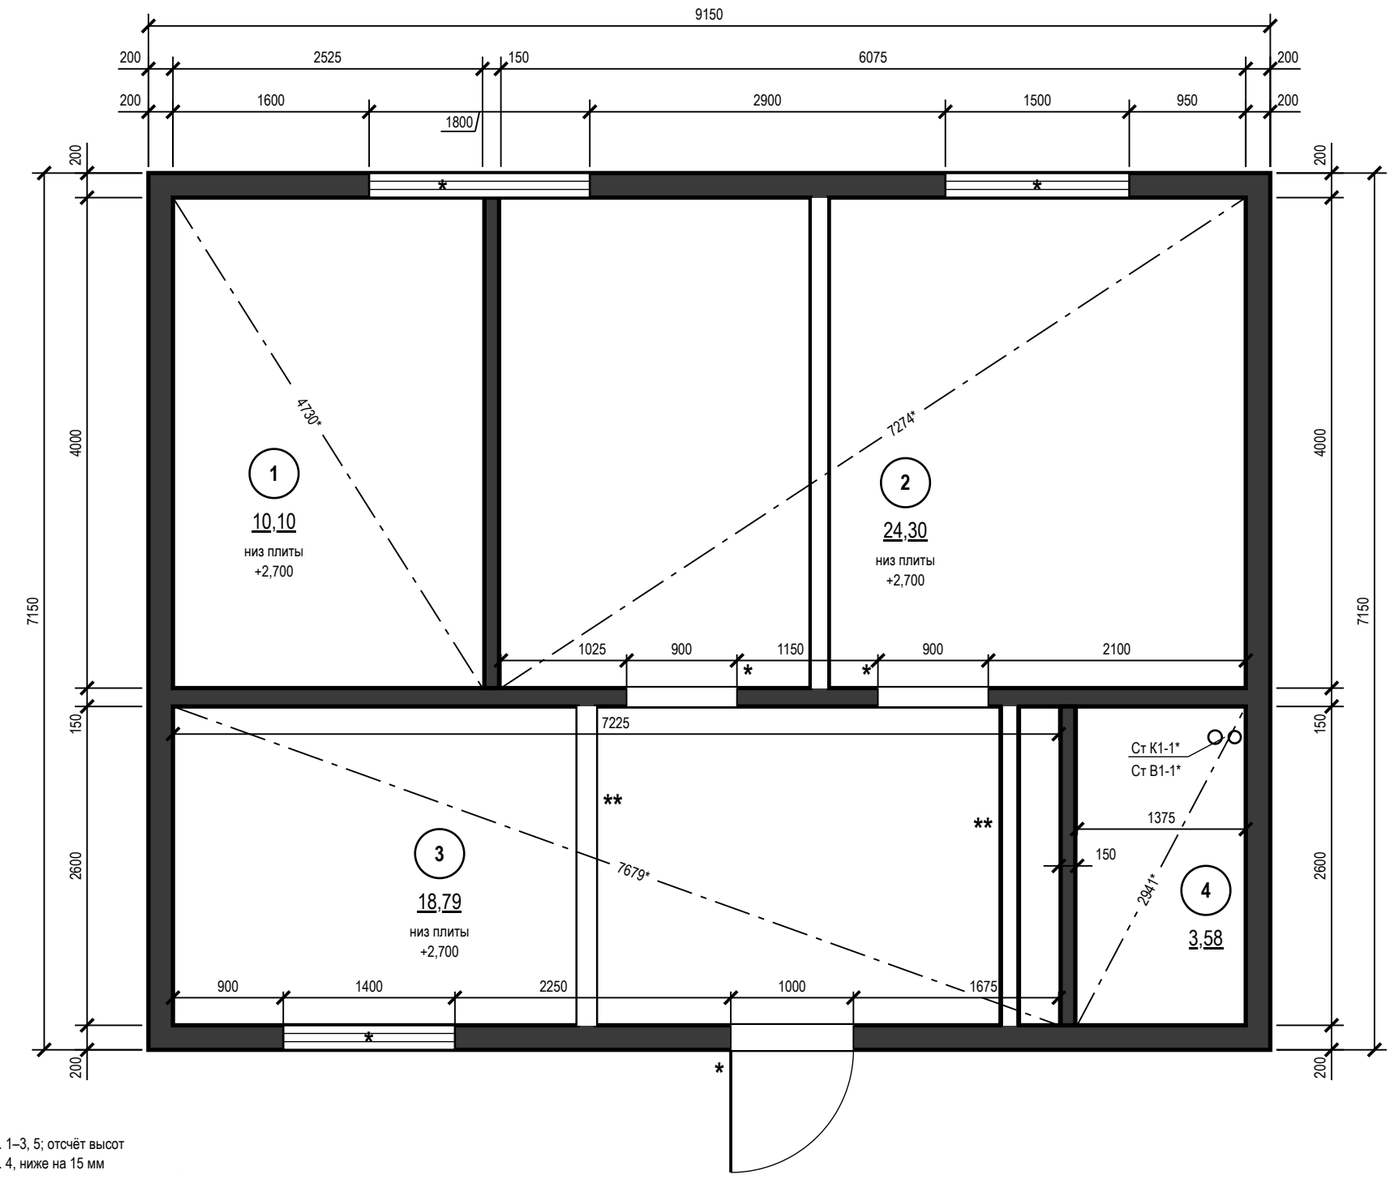

Экспликация помещений

№	Наименование	Площадь, м²
1	Кухня	10,10
2	Гостиная	24,30
3	Прихожая	18,79
4	Санузел	3,58
	Итого (общая площадь)	**56,77**

Условные обозначения

- существующие стены (сечение)
- окно (рама, остекление)
- проём существующий, без заполнения (откосы)
- стояк: К1 — канализация, В1 — ХВС, Т3 — ГВС
- ** — «**» — предложение проектировщика, заказчиком не утверждено
- диагональ помещения — контроль прямоугольности
- (1) — номер помещения, площадь м²
- * — «*» — принято, не замерено и не подтверждено

Примечания

1. Размеры — в мм по чистым поверхностям стен до отделки (по плану заказчика); площади — в м² по тем же размерам. До начала работ выполнить контрольный обмер.
2. Знак «*» у проёма — положение не замерено; реестр: листы 6–7, вопросы К-1, К-11.
3. Знак «*» у стояка — положение принято, не замерено (все стояки); сверить на объекте до разметки. Реестр: листы 6–7, вопрос К-4.
4. За отметку ±0,000 принят чистый пол, не существующий (блок отметок). «Низ плиты» у марки помещения — отметка низа плиты перекрытия от ±0,000, как на развёртках и плане потолков (не высота потолка: потолок — по плану потолков).
5. Толщины стен: наружные 200 мм, перегородки 150 мм; отличающиеся толщины и уступы размерами на плане.
6. Обмер — существующее положение: С-1, С-2 показаны как существующие, их снос — на плане демонтажа; новых конструкций на обмере нет.
7. Помещения и экспликация — до перепланировки (границы и назначение приняты по данным заказчика, не обмерены — К-7). Общая площадь до перепланировки 56,77 м², после — 56,37 м² (экспликация «после» — лист 24); разница −0,40 м² — площадь сносимых и новых перегородок.
8. Несущие стены не определены: до технического заключения все стены считать несущими; проёмы и штробы в них не выполнять.
9. Дверные проёмы показаны без заполнения (двери — лист 25); высота дверных проёмов 2100 мм; низ окон (подоконник) 850, 900 мм от чистого пола, высота окон 1500, 1450 мм.
10. Диагонали — контрольные размеры; «*» — расчёт по принятому контуру (К-1), при обмере заменить замеренным; расхождение более 5 мм подписать на плане как перекос.
11. Размеры проверить на месте до начала работ; расхождение контрольных проверок ≤ 2 %.

Отметки по высоте

±0,000	чистый пол пом. 1–3, 5; отсчёт высот
−0,015	чистый пол пом. 4, ниже на 15 мм
−0,064*	верх плиты — расчёт, не замер (задание на обмер)
сущ. пол	снимается до плиты; не замерен (задание на обмер)

Принято, не определено или спорно

полностью — листы 6–7

К-2 — Высота потолка 2700 мм указана заказчиком в брифе, на объекте не замерена

К-3 — Тип дома (монолитный) и толщина перекрытия 200 мм указаны заказчиком в брифе; проект дома, план БТИ и техническое заключение о несущих конструкциях не переданы

К-7 — Планировка принята по брифу заказчика: положение существующих стен и проёмов, объединение кухни с гостиной (демонтаж С-1), расширение санузла (демонтаж С-2, перегородка П-1**) введены в мастер брифа без обмерного плана и плана БТИ

Допущения и предложения на листе. Основа листа: размеры помещений и положение проёмов введены заказчиком в брифе, на объекте не замерены (К-1); высота потолка 2700 мм — по брифу заказчика, не замерена (К-2); толщины стен приняты по брифу: наружные 200 мм, внутренние 150 мм — не обмерены (К-1); тип дома монолитный, перекрытие 200 мм — по брифу заказчика, документов нет (К-3); планировка (стены, проёмы, объединение кухни и гостиной, расширение санузла) — по брифу без обмера и плана БТИ (К-7); разрешённая мощность 10 кВт принята, ТУ не переданы (К-8); вентканалы приняты, в брифе не заданы (К-9); подрайон климата не задан — принят не северный (жилые от 2,5 м) (К-10). Знак «*» — принято, не замерено и не подтверждено (замерить на объекте): К-4: Ст К1-1 — положение стояка канализации — по брифу заказчика, не замерено; Ст В1-1 — положение стояка холодной воды — по брифу заказчика, не замерено. Знак «**» — предложение проектировщика, заказчиком не утверждено (согласовать с заказчиком): К-5: П-1 — положение, материал (пеноблок) и толщина 100 мм — по брифу заказчика; конструкция (кладка, армирование, штукатурка) — выбор исполнителя, автором не утверждена; кладка — не ГКЛ: каркас, листы и Rw системы не считаются (система, лист, слои, Rw — «—»). См. лист открытых вопросов (лист 6, записи К-1–К-5, К-7–К-10); по листу — К-1–К-3, К-7.

1000 мм · печать 1:1

Изм.	Кол.уч	Лист	№ док.	Подп.	Дата
Разраб.		Кырлан А.С.			13.11.26
Пров.					
ГИП					
Н. контр.					
Утв.					

ГД-2026-011-АИ

Квартира 56 м²

ЖК «Северный парк», Москва

Дизайн-проект интерьера

Стадия	Лист	Листов
РП	21	119

Обмерный план

М 1:50

Кырлан Александр Сергеевич


выпуск 13.11.2026 № eb7810814f · стр. 22 из 139

План демонтажа и монтажа перегородок

Существующее — серым, демонтаж — красным, монтаж — синим · размеры в мм

ПРЕДВАРИТЕЛЬНО · не для производства работ · открыто пунктов: 13 (реестр — л. 6, 7)

Допущения и предложения на листе. Основа листа: размеры помещений и положение проёмов введены заказчиком в брифе, не замерены (К-1); высота потолка 2700 мм — по брифу заказчика, не замерена (К-2); толщины стен приняты по брифу: наружные 200 мм, внутренние 150 мм — не обмерены (К-1); тип дома монолитный, перекрытие 200 мм — по брифу заказчика, документов нет (К-3); планировка (стены, проёмы, объединение кухни и гостиной, расширение санузла) — по брифу без обмера и плана БТИ (К-7); разрешённая мощность 10 кВт принята, ТУ не переданы (К-8); вентканалы приняты, в брифе не заданы (К-9); подрайон климата не задан — принят не северный (жилые от 2,5 м) (К-10). Знак «*» — принято, не замерено (замерить). Знак «**» — предложено, не утверждено (согласовать): К-5: П-1, П-2, П-3. См. лист открытых вопросов (лист 6, записи К-1–К-3, К-5, К-7–К-10).

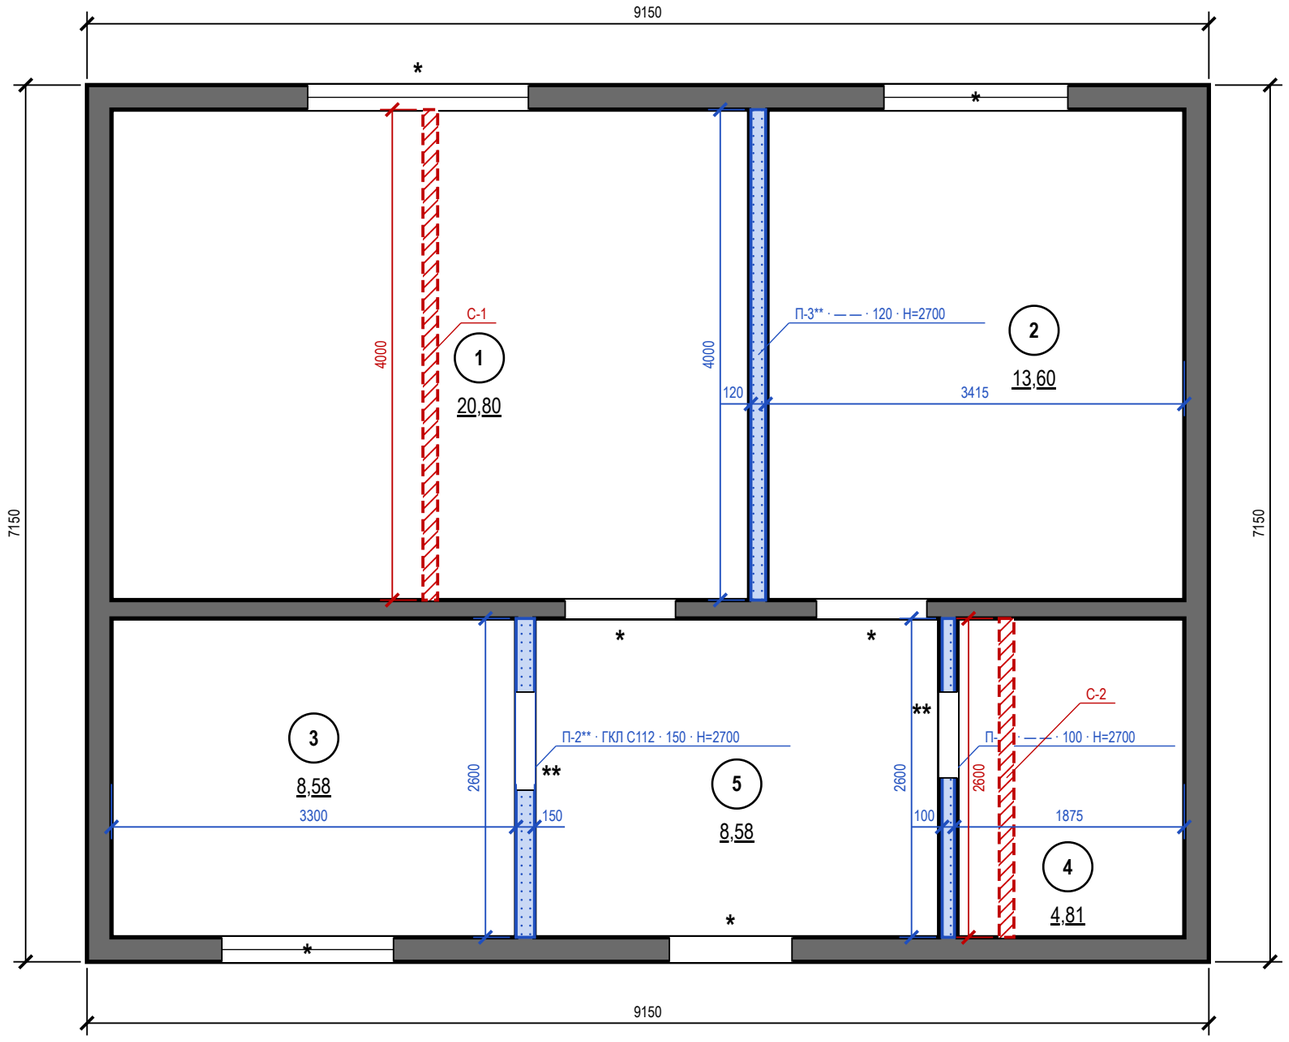


Ведомость демонтажа и монтажа

Марка	Конструкция	Длина, мм	Толщ., мм	Высота	Примечание
С-1	демонтаж: перегородка	4000	120	2700	перегородка кухня/гостиная, объединение в кухню-гостиную
С-2	демонтаж: перегородка	2600	120	2700	старая стена санузла, расширение мокрой зоны
П-1**	монтаж: Пеноблок D500, армирование через 2 ряда, штукатурка с двух сторон,	2600	100	Н=2700	новая стена санузла, пеноблок под гидроизоляцию
П-2**	монтаж: ГКЛ 12,5 мм в 2 слоя с каждой стороны по металлическому каркасу ПС/ПН, минеральная вата 50 мм, С112	2600	150	Н=2700	перегородка детская/прихожая, ГКЛ со звукоизоляцией
П-3**	монтаж: Кирпич керамический полнотелый, кладка в полкирпича, штукатурка с двух сторон,	4000	120	Н=2700	перегородка спальня/гостиная, кирпич для звукоизоляции

Условные обозначения

- существующие стены — сохраняются;
- несущие не определены — считать несущими
- демонтируемые конструкции (красным)
- новое — возводится по проекту (синим)
- ** — «**» — предложение проектировщика, заказчиком не утверждено
- проём существующий, без заполнения (откосы)
- 1 — номер помещения, площадь м²
- * — «*» — принято, не замерено и не подтверждено

Отметки по высоте

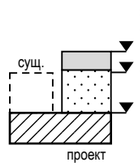

±0,000	чистый пол пом. 1–3, 5; отсчёт высот
−0,015	чистый пол пом. 4, ниже на 15 мм
−0,064*	верх плиты — расчёт, не замер (задание на обмер)
сущ. пол	снимается до плиты; не замерен (задание на обмер)

Примечания

1. Демонтаж несущих стен и плит перекрытия не производится; снос несущих конструкций — только по техническому заключению (в ведомости).
2. Новые перегородки и фальш-стены (синим) привязаны от капитальных стен и наружного контура; высота — по ведомости («до плиты» — до низа плиты перекрытия); проёмы в них усилить стойками каркаса.
3. Знак «**» — предложение проектировщика, заказчиком не утверждено (согласовать с заказчиком) у конструкций (вопрос К-5): до решения не возводить. На обмерном плане их нет.
4. Перепланировку согласовать до начала работ (ЖК РФ, ст. 26); план не передавать в работу до допуска главного инженера проекта.
5. Дверные блоки — по плану дверей (лист 25); существующие проёмы не расширяются.
6. Знак «*» — положение проёма не замерено: окна пом. 1, 2, 3; двери пом. 1, 2, 5. Реестр: листы 6–7, вопросы К-1, К-11.
7. Демонтаж существующих покрытий пола, стен и потолка, дверных блоков и сантехприборов (если есть) — до основания; объёмы демонтажа — для справки, по факту на объекте.
8. За отметку ±0,000 принят чистый пол, не существующий (блок отметок). Размеры — в мм по чистовой поверхности стен до отделки.
9. Размеры проверить на месте до начала работ: расхождение с обмером — не более 2 % (иначе — к архитектору).
10. Несущие стены не определены: до технического заключения все стены считать несущими — проёмы, ниши и штробы в них не выполнять.

1000 мм · печать 1:1

Изм.	Кол.уч	Лист	№ док.	Подп.	Дата
Разраб.		Кырлан А.С.			13.11.26
Пров.					
ГИП					
Н. контр.					
Утв.					

ГД-2026-011-АИ

Квартира 56 м²

ЖК «Северный парк», Москва

Дизайн-проект интерьера

Стадия	Лист	Листов
РП	22	119

План демонтажа и монтажа перегородок


М 1:50

Кырлан Александр Сергеевич

выпуск 13.11.2026 № eb7810814f · стр. 23 из 139

План демонтажа


Существующее — серым, демонтаж — красным; новых конструкций на листе нет · размеры в мм

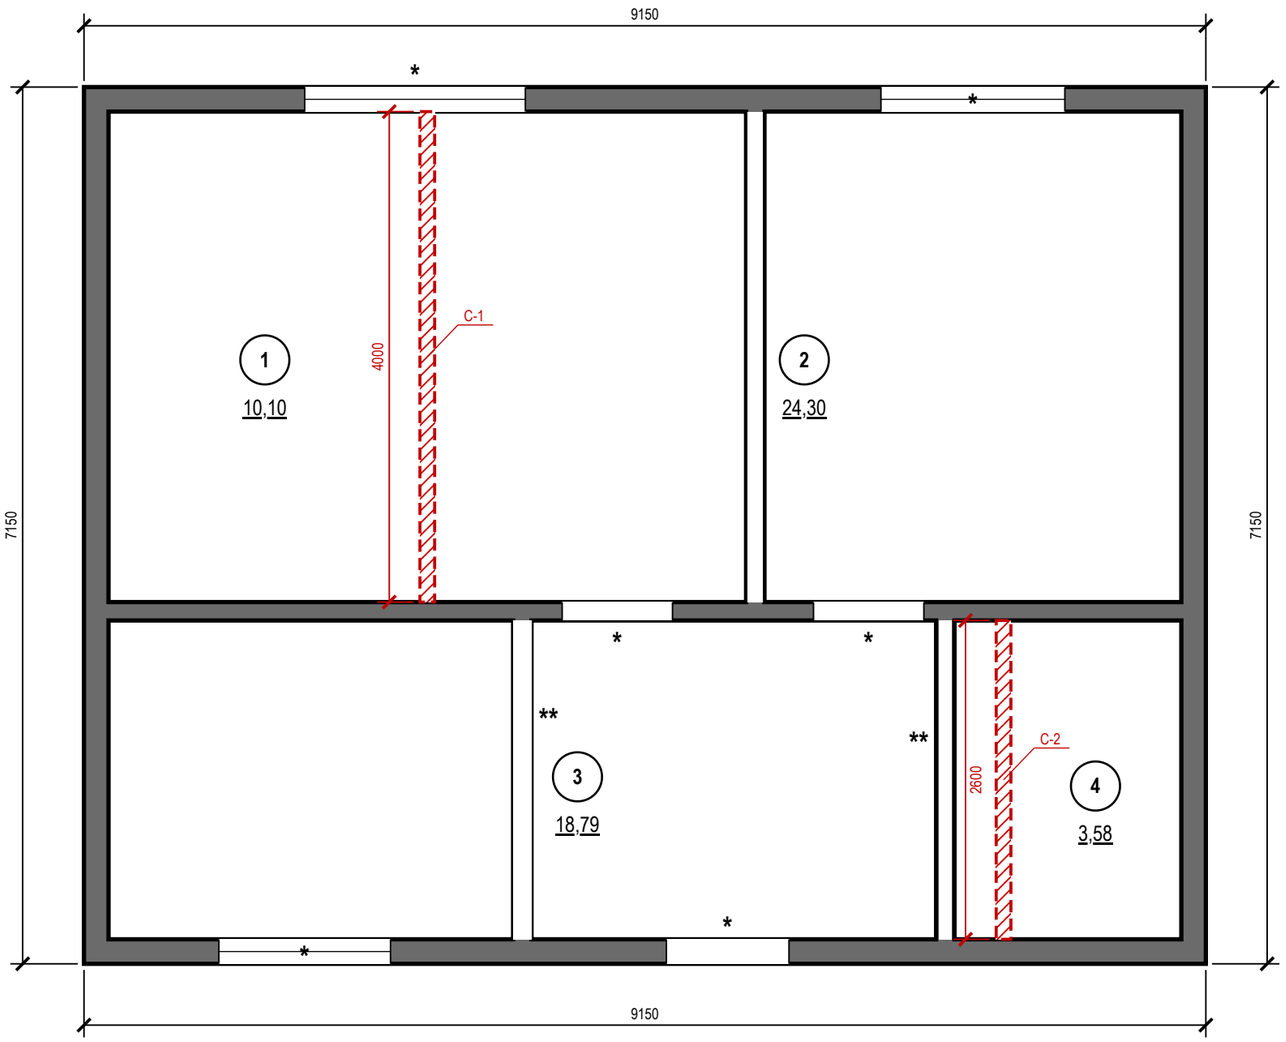

Условные обозначения

- существующие стены — сохраняются;
- несущие не определены — считать несущими
- демонтируемые конструкции (красным)
- проём существующий, без заполнения (откосы)
- (1) номер помещения, площадь м²
- * «*» — принято, не замерено и не подтверждено

Отметки по высоте

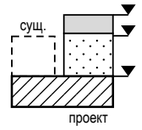

±0,000	чистый пол пом. 1–3, 5; отсчёт высот
−0,015	чистый пол пом. 4, ниже на 15 мм
−0,064*	верх плиты — расчёт, не замер (задание на обмер)
сущ. пол	снимается до плиты; не замерен (задание на обмер)

Допущения и предложения на листе

Основа листа: размеры помещений и положение проёмов введены заказчиком в брифе, на объекте не замерены (К-1); высота потолка 2700 мм — по брифу заказчика, не замерена (К-2); толщины стен приняты по брифу: наружные 200 мм, внутренние 150 мм — не обмерены (К-1); тип дома монолитный, перекрытие 200 мм — по брифу заказчика, документов нет (К-3); планировка (стены, проёмы, объединение кухни и гостиной, расширение санузла) — по брифу без обмера и плана БТИ (К-7); разрешённая мощность 10 кВт принята, ТУ не переданы (К-8); вентканалы приняты, в брифе не заданы (К-9); подрайон климата не задан — принят не северный (жилые от 2,5 м) (К-10).

Знак «*» — принято, не замерено и не подтверждено (замерить на объекте): К-1: окно пом. 1 (стена А) — окно: положение, ширина, высота и подоконник — по брифу заказчика, не замерены; ограждение 900 мм — предложение исполнителя; дверь пом. 1 (стена В) — Петли у правого откоса (х 4600): открытое полотно стоит у стены Б, вошедший идёт влево к кухне; при петлях слева полотно запирало вход в карман между собой, диваном Гс2 и стеной Б; окно пом. 2 (стена А), 3 (В) — окно: положение, ширина, высота и подоконник — по брифу заказчика, не замерены; дверь пом. 2 (стена В) — проём в существующей стене между пом. 2 и 5: положение и ширина — по брифу заказчика, не замерены; дверь пом. 5 (стена В) — входная дверь: положение и ширина проёма — по брифу заказчика, не замерены.

Знак «**» — предложение проектировщика, заказчиком не утверждено (согласовать с заказчиком): К-5: дверь пом. 3 (стена Б), 4 (Г) — дверь в новой перегородке: проём по брифу, короб скрытой двери и размер в свету — после выбора модели и утверждения перегородки (К-5).

См. лист открытых вопросов (лист 6, записи К-1–К-3, К-5, К-7–К-10).

Примечания

1. План демонтажа — фильтр «существующее + демонтаж»: новых конструкций на листе нет (они — на плане монтажа); ведомость демонтажа и монтажа — на листе «План демонтажа и монтажа перегородок».
2. Демонтаж несущих стен и плит перекрытия не производится; снос несущих конструкций — только по техническому заключению (в ведомости).
3. Перепланировку согласовать до начала работ (ЖК РФ, ст. 26); план не передавать в работу до допуска главного инженера проекта.
4. Дверные блоки — по плану дверей (лист 25); существующие проёмы не расширяются.
5. Знак «*» — положение проёма не замерено: окна пом. 1, 2, 3; двери пом. 1, 2, 5. Реестр: листы 6–7, вопросы К-1, К-11.
6. Демонтаж существующих покрытий пола, стен и потолка, дверных блоков и сантехприборов (если есть) — до основания; объёмы демонтажа — для справки, по факту на объекте.
7. За отметку ±0,000 принят чистый пол, не существующий (блок отметок). Размеры — в мм по чистовой поверхности стен до отделки.
8. Размеры проверить на месте до начала работ: расхождение с обмером — не более 2 % (иначе — к архитектору).
9. Несущие стены не определены: до технического заключения все стены считать несущими — проёмы, ниши и штробы в них не выполнять.
10. Марки помещений — до перепланировки (экспликация — на обмерном плане).

1000 мм · печать 1:1

Изм.	Кол.уч	Лист	№ док.	Подп.	Дата
Разраб.		Кырлан А.С.			13.11.26
Пров.					
ГИП					
Н. контр.					
Утв.					

ГД-2026-011-АИ

Квартира 56 м²

ЖК «Северный парк», Москва

Дизайн-проект интерьера

Стадия	Лист	Листов
РП	23	119

План демонтажа

М 1:50

Кырлан Александр Сергеевич


выпуск 13.11.2026 № eb7810814f · стр. 24 из 139

План монтажа перегородок

Существующее после демонтажа — серым, монтаж — синим; снесённого на листе нет · размеры в мм

ПРЕДВАРИТЕЛЬНО · не для производства работ · открыто пунктов: 13 (реестр — л. 6, 7)


Допущения и предложения на листе. Основа листа: размеры помещений и положение проёмов введены заказчиком в брифе, не замерены (К-1); высота потолка 2700 мм — по брифу заказчика, не замерена (К-2); толщины стен приняты по брифу: наружные 200 мм, внутренние 150 мм — не обмерены (К-1); тип дома монолитный, перекрытие 200 мм — по брифу заказчика, документов нет (К-3); планировка (стены, проёмы, объединение кухни и гостиной, расширение санузла) — по брифу без обмера и плана БТИ (К-7); разрешённая мощность 10 кВт принята, ТУ не переданы (К-8); вентканалы приняты, в брифе не заданы (К-9); подрайон климата не задан — принят не северный (жилые от 2,5 м) (К-10). Знак «*» — принято, не замерено (замерить). Знак «**» — предложено, не утверждено (согласовать): К-5: П-1, П-2, П-3. См. лист открытых вопросов (лист 6, записи К-1–К-3, К-5, К-7–К-10).

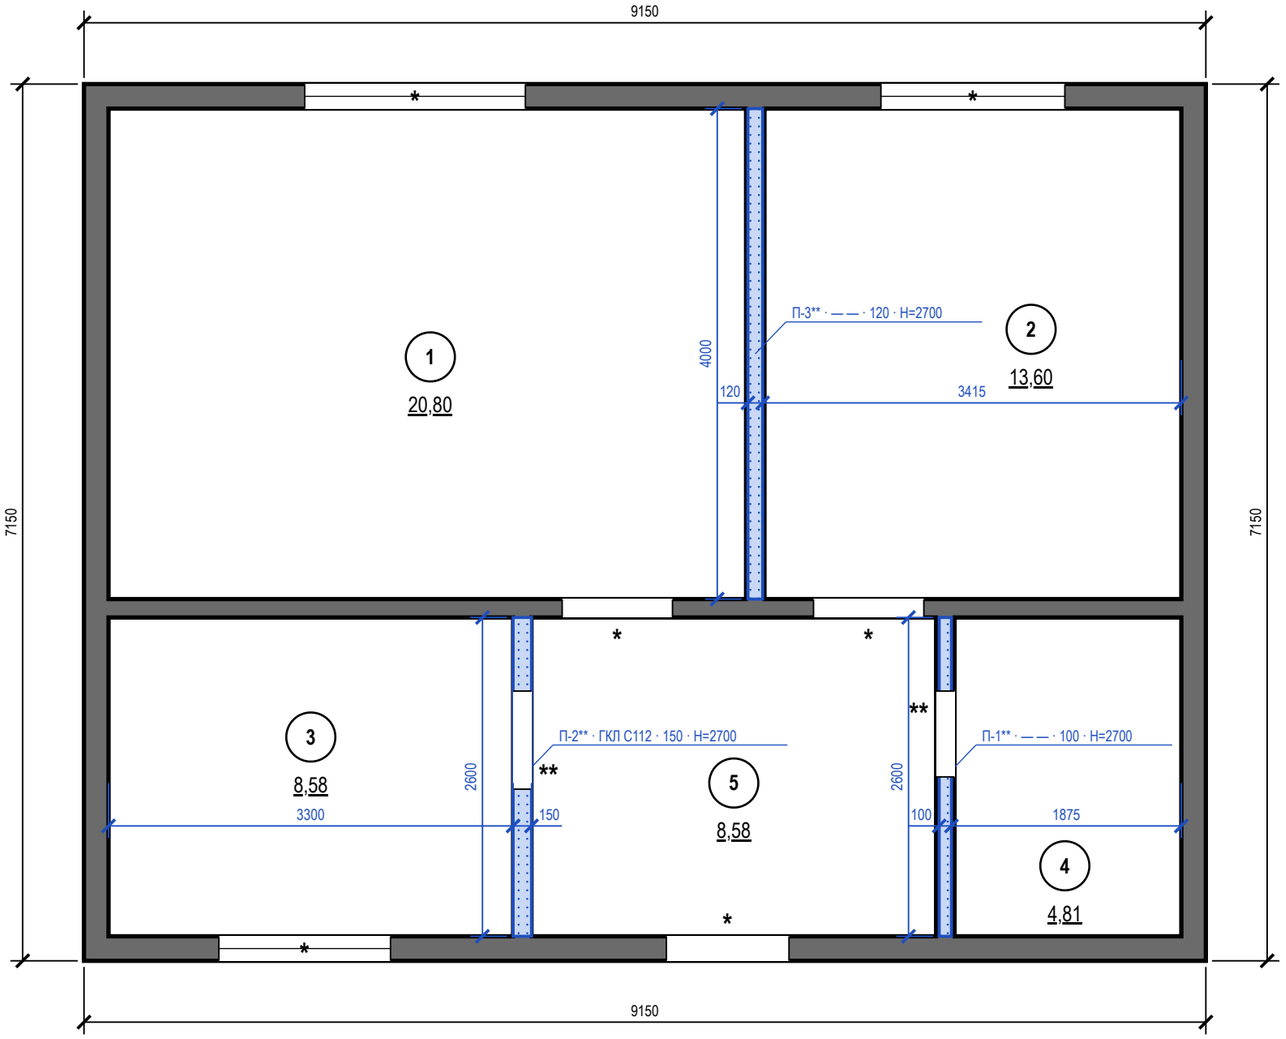

Условные обозначения

- существующие стены — сохраняются; несущие не определены — считать несущими
- новое — возводится по проекту (синим)
- ** — «**» — предложение проектировщика, заказчиком не утверждено
- проём существующий, без заполнения (откосы)
- 1 — номер помещения, площадь м²
- * — «*» — принято, не замерено и не подтверждено

Отметки по высоте

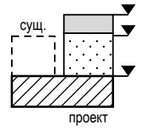

±0,000	чистый пол пом. 1–3, 5; отсчёт высот
−0,015	чистый пол пом. 4, ниже на 15 мм
−0,064*	верх плиты — расчёт, не замер (задание на обмер)
сущ. пол	снимается до плиты; не замерен (задание на обмер)

Экспликация помещений (после перепланировки)

№	Наименование	Площадь, м²
1	Гостиная-кухня	20,80
2	Спальня	13,60
3	Детская	8,58
4	Санузел	4,81
5	Прихожая	8,58
	Итого (общая площадь)	**56,37**

Примечания

1. План монтажа — фильтр «существующее после демонтажа + новое»: снесённых конструкций на листе нет (они — на плане демонтажа); ведомость демонтажа и монтажа — на листе «План демонтажа и монтажа перегородок».
2. Демонтаж несущих стен и плит перекрытия не производится.
3. Новые перегородки и фальш-стены (синим) привязаны от капитальных стен и наружного контура; высота — по ведомости («до плиты» — до низа плиты перекрытия); проёмы в них усилить стойками каркаса.
4. Знак «**» — предложение проектировщика, заказчиком не утверждено (согласовать с заказчиком) у конструкций (вопрос К-5): до решения не возводить. На обмерном плане их нет.
5. Перепланировку согласовать до начала работ (ЖК РФ, ст. 26); план не передавать в работу до допуска главного инженера проекта.
6. Дверные блоки — по плану дверей (лист 25); существующие проёмы не расширяются.
7. Знак «*» — положение проёма не замерено: окна пом. 1, 2, 3; двери пом. 1, 2, 5. Реестр: листы 6–7, вопросы К-1, К-11.
8. Демонтаж существующих покрытий пола, стен и потолка, дверных блоков и сантехприборов (если есть) — до основания; объёмы демонтажа — для справки, по факту на объекте.
9. За отметку ±0,000 принят чистый пол, не существующий (блок отметок). Размеры — в мм по чистовой поверхности стен до отделки.
10. Размеры проверить на месте до начала работ: расхождение с обмером — не более 2 % (иначе — к архитектору).
11. Несущие стены не определены: до технического заключения все стены считать несущими — проёмы, ниши и штробы в них не выполнять.
12. Экспликация на листе — после перепланировки; до перепланировки — на обмерном плане (лист 21). Общая площадь до 56,77 м², после 56,37 м²; разница −0,40 м² — площадь сносимых и новых перегородок.

1000 мм · печать 1:1

Изм.	Кол.уч	Лист	№ док.	Подп.	Дата
Разраб.		Кырлан А.С.			13.11.26
Пров.					
ГИП					
Н. контр.					
Утв.					

ГД-2026-011-АИ

Квартира 56 м²

ЖК «Северный парк», Москва

Дизайн-проект интерьера

Стадия	Лист	Листов
РП	24	119

План монтажа перегородок


М 1:50

Кырлан Александр Сергеевич

выпуск 13.11.2026 № eb7810814f · стр. 25 из 139

План дверей и ведомость заполнения проёмов

Проёмы, марки заполнения, привязки · размеры в мм

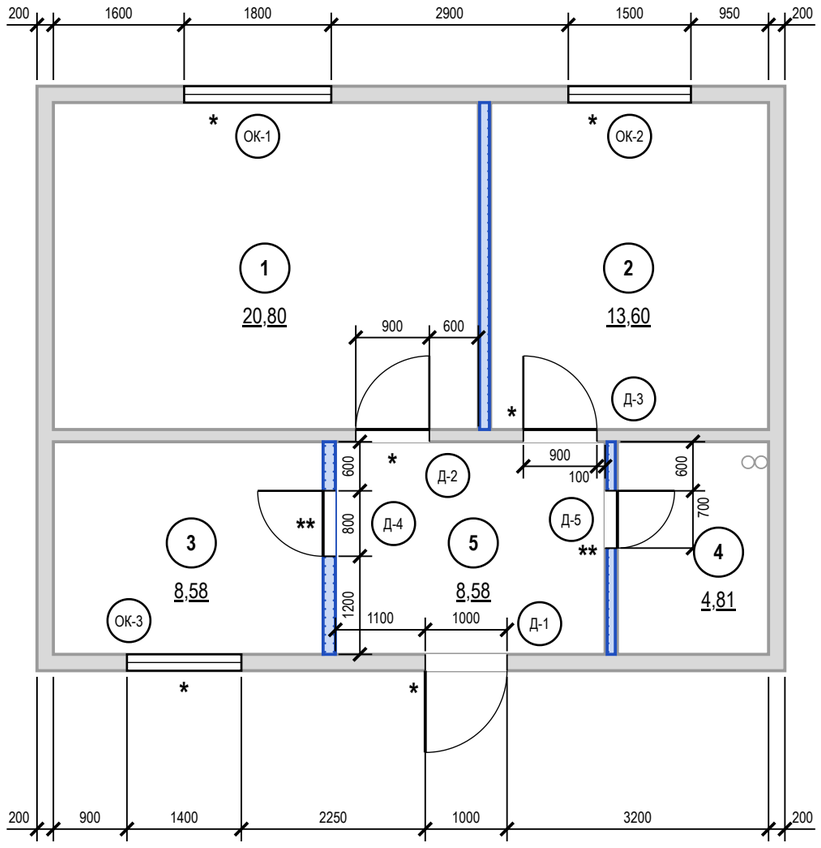

Ведомость заполнения проёмов

Марка	Наименование, обозначение	Проём ш×в, мм	Полотно (расч.)	Кол.	Откр.	Отделка полотна	Фурнитура	Прим.
Д-1	Блок дверной входной, ГОСТ 31173-2016	1000×2100	блок задать	1	Л	в комплекте блока	в комплекте блока (замки, глазок)	* пом. 5; наружу
Д-2	Дверь скрытого монтажа, UNION FILO-60 Piatto	900×2100	800×2000	1	Л	окраска S 0804-Y30R с двух сторон	скрытые петли 3D, магнитный замок	* пом. 1
Д-3	Дверь скрытого монтажа, UNION FILO-60 Piatto	900×2100	800×2000	1	П	окраска S 0804-Y30R с двух сторон	скрытые петли 3D, магнитный замок	* пом. 2
Д-4	Дверь скрытого монтажа, UNION FILO-60 Piatto	800×2100	700×2000	1	Л	окраска S 0804-Y30R с двух сторон	скрытые петли 3D, магнитный замок	** пом. 3
Д-5	Дверь скрытого монтажа, UNION FILO-60 Piatto	700×2100	600×2000	1	П	в тон облицовки — пом. 4, S 0804-Y30R — пом. 5	скрытые петли 3D, магнитный замок, фиксатор WC	** пом. 4; порог 15
ОК-1	Блок оконный, ГОСТ 23166-2021	1800×1500		1				* пом. 1; низ 850
ОК-2	Блок оконный, ГОСТ 23166-2021	1500×1450		1				* пом. 2; низ 900
ОК-3	Блок оконный, ГОСТ 23166-2021	1400×1450		1				* пом. 3; низ 900

Условные обозначения

- стены (подложка обмера)
- новое — возводится по проекту (синим)
- дверь распашная, дуга открывания
- дверь скрытого монтажа
- дверь входная (полотно толще)
- оконный блок
- Д — марка типа (Д-N, ОК-N)
- 1 — номер помещения, площадь м²
- * — «*» — принято, не замерено и не подтверждено
- ** — «**» — предложение проектировщика, заказчиком не утверждено

Допущения и предложения на листе. Основа листа: размеры помещений и положение проёмов введены заказчиком в брифе, на объекте не замерены (К-1); высота потолка 2700 мм — по брифу заказчика, не замерена (К-2); толщины стен приняты по брифу: наружные 200 мм, внутренние 150 мм — не обмерены (К-1); тип дома монолитный, перекрытие 200 мм — по брифу заказчика, документов нет (К-3); планировка (стены, проёмы, объединение кухни и гостиной, расширение санузла) — по брифу без обмера и плана БТИ (К-7); разрешённая мощность 10 кВт принята, ТУ не переданы (К-8); вентканалы приняты, в брифе не заданы (К-9); подрайон климата не задан — принят не северный (жилые от 2,5 м) (К-10). Знак «*» — принято, не замерено и не подтверждено (замерить на объекте): К-4: Ст К1-1 — положение стояка канализации — по брифу заказчика, не замерено; Ст В1-1 — положение стояка холодной воды — по брифу заказчика, не замерено. Знак «**» — предложение проектировщика, заказчиком не утверждено (согласовать с заказчиком): К-5: П-1 — положение, материал (пеноблок) и толщина 100 мм — по брифу заказчика; конструкция (кладка, армирование, штукатурка) — выбор исполнителя, автором не утверждена; кладка — не ГКЛ: каркас, листы и Rw системы не считаются (система, лист, слои, Rw — «—»); П-2 — положение, материал (ГКЛ) и толщина 150 мм — по брифу заказчика; конструкция (система С112, 2 слоя с каждой стороны, Rw 51 дБ — нижняя граница диапазона системы С112 (51–56 дБ)) — выбор исполнителя, автором не утверждена; П-3 — положение, материал (кирпич) и толщина 120 мм — по брифу заказчика; конструкция (кладка, армирование, штукатурка) — выбор исполнителя, автором не утверждена; кладка — не ГКЛ: каркас, листы и Rw системы не считаются (система, лист, слои, Rw — «—»). См. лист открытых вопросов (лист 6, записи К-1–К-5, К-7–К-10); по листу — К-1.

Примечания

1. Размеры проёмов и привязки — в миллиметрах от чистых граней стен до отделки; привязка — от угла того помещения, со стороны которого стоит размер. Размер проёма — ширина × высота от чистого пола 0,000. Размеры на плане — проёмов, не полотен: полотно — в ведомости, коробка — по системе. Откос от угла помещения до проёма с коробкой — не менее 50 мм.
2. Марки в кружках — типы заполнения проёмов (ГОСТ 21.501-2018, п. 5.3.2); одна марка — один типоразмер; количество сверено с планом.
3. Открывание: Л — петли слева, П — справа, если смотреть со стороны, куда открывается полотно (на себя).
4. Скрытые двери (Д-2…Д-5): проём замерить в чистоте; блок заказать до штукатурки (≈ 30 дн.), короб ставить до штукатурки; полотно навесить после чистовой отделки, красить в цвет стен. Порядок — практика монтажа, изготовитель подтверждает.
5. Д-2, Д-3 — существующие проёмы, до техзаключения не расширять (К-1).
6. Полотно «расч.» — по проёму и ряду изделия с запасом по каталогам, заказ — по таблице проёмов модели; Д-2…Д-5: проём 2100, а под полотно 2000 по каталогам нужен 2050–2080, под 2100 — 2150–2180: высоту проёма — по модели; Д-1: входной блок по ГОСТ 31173-2016 — задать при выборе блока.
7. Д-1: дуга наружу — по плану заказчика, не проверено; блок оставить или заменить — не решено (К-1).
8. Знак «*» у проёма — допущение: положение проёма не замерено (окно пом. 1, стена А; дверь пом. 1, стена В; окно пом. 2, стена А; дверь пом. 2, стена В; окно пом. 3, стена В; дверь пом. 5, стена В); размер напечатан как принятый; в ведомости — знак «*» в графе «Прим.». Реестр: листы 6–7, вопросы К-1, К-11.
9. Экспликация помещений после перепланировки — лист 24; в марках помещений — номер и площадь, м².

1000 мм · печать 1:1

Изм.	Кол.уч	Лист	№ док.	Подп.	Дата			
Разраб.		Кырлан А.С.			13.11.26	ГД-2026-011-АИ		
Пров.						Квартира 56 м² ЖК «Северный парк», Москва		
ГИП						Дизайн-проект интерьера	Стадия: РП	Лист: 25 / Листов: 119
Н. контр.						План дверей и ведомость заполнения проёмов М 1:75	Кырлан Александр Сергеевич	
Утв.								

выпуск 13.11.2026 № eb78108814f · стр. 26 из 139

02

Планировочное решение

Кырлан Александр Сергеевич

выпуск 13.11.2026 21 eb7810814f · стр. 27 из 139


Концепция интерьера

Джапанди · схема аналоговая · 60/30/10 · материалы, образы и зонирование


Идея

Джапанди для пары с ребёнком 6 лет и котом: низкая мебель, два тона дерева (дуб и тёмный ясень), матовые тёплые нейтрали, серо-зелёный второй план, одна картина на комнату. Кухня линейная у стены Г с навесными шкафами, стол у окна, ТВ-зона с низкой консолью; рабочее место в спальне; шкаф-купе и антресоль в прихожей; скрытые двери, шторы в нише потолка; без глянца и холодного белого. Стиль — джапанди: тишина, заземлённость, медленная жизнь, тёплый минимализм, ваби-саби, hygge. Стены S 0804-Y30R, потолок Damask F485, серо-зелёный Sea Smoke и дуб под маслом, акценты — олива Bancha и тёмный орех; без глянца (К-6). Цветовая схема — аналоговая, пропорция 60/30/10: база на стенах и потолках, вторичный цвет — в текстиле и мягкой мебели, акцент — точечно.

Мудборд: материалы и фактуры

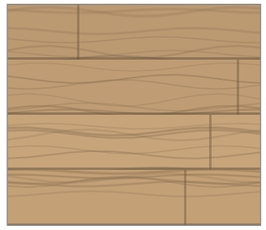

1167-1101
пол

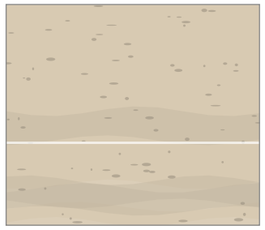

Керамогранит под травертин
фартук



Damask · Tikkurila F485
потолок



NCS S 0804-Y30R
стены, плинтус




Bancha · Farrow & Ball No. 298
акцент (стена А)




NCS S 5010-G70Y
акцент (стена А)



Sea Smoke · Tikkurila X447
акцент (стена Г)

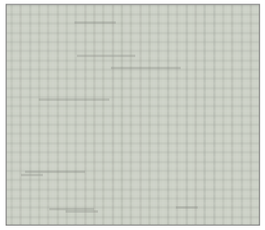

Лён, Tikkurila X447
портьеры-волна, подушки декоративные на кровать

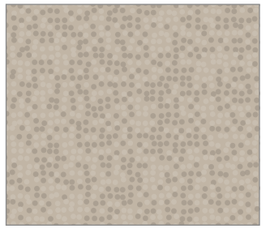

Шерсть, Tikkurila V484
ковёр в зоне отдыха, плед на диван

Палитра 60/30/10




60 % база — NCS S 0804-Y30R, LRV 78; Tikkurila F485 Damask, LRV 83

30 % вторичный — Tikkurila X447 Sea Smoke, LRV 63; Tikkurila V484 Driftwood, LRV 47; NCS S 2005-Y30R, LRV 55

10 % акцент — Farrow & Ball No. 298 Bancha, LRV 14; NCS S 5010-G70Y, LRV 22; NCS S 7005-Y20R, LRV 9

Функциональное зонирование (М 1:100)

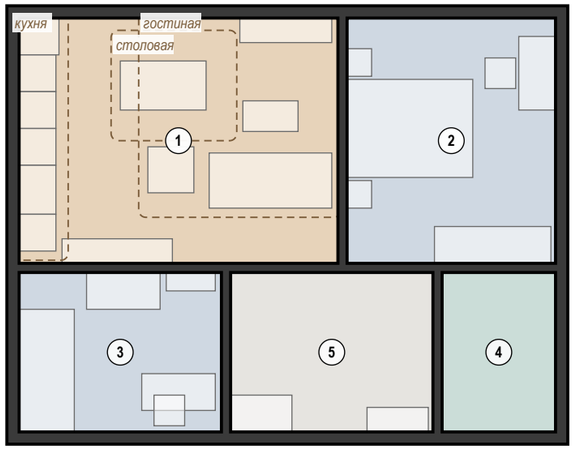

дневная зона: гостиная, кухня, столовая
ночная зона: спальни
мокрая зона: санузлы
вход и коммуникации
функциональная зона в помещении
1 номер помещения (лист 27)

Образы помещений

1. Гостиная-кухня 20,80 м²

стены NCS S 0804-Y30R; акцент No. 298 на стене А
пол — 1167-1101
текстиль: портьеры X447, тюль F485, ковёр в зоне отдыха V484
декор: картина над консолью, Фикус

2. Спальня 13,60 м²

стены NCS S 0804-Y30R; акцент S 5010-G70Y на стене А
пол — 1167-1101
текстиль: портьеры X447, тюль F485, ковёр S 2005-Y30R
декор: картина над кроватью, реечная панель,

3. Детская 8,58 м²

стены NCS S 0804-Y30R; акцент X447 на стене Г
пол — 1167-1101
текстиль: портьеры X447, тюль F485, ковёр игровой V484
декор: картина над кроватью, зеркало в рост, лампа настольная рабочая

5. Прихожая 8,58 м²

стены NCS S 0804-Y30R
пол — A8UZ
декор: зеркало над скамьёй, графика в раме
свет 3000/2700 K

4. Санузел 4,81 м²

стены Atlas Concorde A8UZ
пол — керамогранит под травертин, матовый
текстиль: полотенца банные махровые S 5010-G70Y, полотенца для рук вафельные F485, коврик для ванной у бортика ванны S 2005-Y30R
декор: зеркало над умывальником, ваза-бутыль

Материалы и отделка

1167-1101
пол — пом. 1, 2, 3

Керамогранит под травертин
матовый; 1200×600
фартук — пом. 1

Керамогранит ректифицированный под травертин
матовый; 600×600
пол — пом. 4

A8UZ
стены, пол — пом. 4, 5

NCS S 0804-Y30R, LRV 78
Tikkurila Euro Power 7, колеровка по NCS, матовая
стены, плинтус — пом. 1, 2, 3, 5

Tikkurila F485 Damask, LRV 83
Tikkurila Euro Power 7, глубокоматовая
потолок — пом. 1, 2, 3, 4, 5

Farrow & Ball No. 298 Bancha, LRV 14
акцентная стена
акцент (стена А) — пом. 1

NCS S 5010-G70Y, LRV 22
акцентная стена
акцент (стена А) — пом. 2

Tikkurila X447 Sea Smoke, LRV 63
акцентная стена
акцент (стена Г) — пом. 3

Текстиль и металл

Лён, Tikkurila X447
портьеры-волна, подушки декоративные на кровать

Шерсть, Tikkurila V484
ковёр в зоне отдыха, плед на диван

Бархат, Farrow & Ball No. 298
подушки на диван

Бархат, NCS S 5010-G70Y
подушки на кровать

Букле, NCS S 1002-Y50R
подушки декоративные на кровать

Вуаль, Tikkurila F485
тюль

Букле, Tikkurila X447
подушки на диван

Шерсть, NCS S 2005-Y30R
ковёр под кроватью, коврик для ванной у бортика ванны

Шерсть, NCS S 5010-G70Y
плед на кровать

Бархат, Tikkurila X447
подушки на кровать

Чего избегаем

1) Бежевое всё без контраста светлого и тёмного
2) Японские сувениры: веера, иероглифы, сакура-принты, катаны, Будды
3) Холодные серые, чистый белый, свет 4000 K+
4) Три-четыре породы и тона дерева, глянцевые плёнки под дерево
5) Много мелкого декора, заставленные открытые полки
6) Искусственные растения и лампасная трава как единственный декор

Допущения и предложения на листе

Основа листа: размеры помещений и положение проёмов введены заказчиком в брифе, на объекте не замерены (К-1); высота потолка 2700 мм — по брифу заказчика, не замерена (К-2); толщины стен приняты по брифу: наружные 200 мм, внутренние 150 мм — не обмерены (К-1); тип дома монолитный, перекрытие 200 мм — по брифу заказчика, документов нет (К-3); планировка (стены, проёмы, объединение кухни и гостиной, расширение санузла) — по брифу без обмера и плана БТИ (К-7); разрешённая мощность 10 кВт принята, ТУ не переданы (К-8); вентканалы приняты, в брифе не заданы (К-9); подрайон климата не задан — принят не северный (жилые от 2,5 м) (К-10).
См. лист открытых вопросов (лист 6, записи К-1–К-3, К-7–К-10).

Примечания

1. Коды цвета — по веерам производителей (колерная карта, лист 62); перед закупкой краски — выкрас на стене объекта под дневным светом и лампами проекта.
2. Материалы — по ведомости отделки (лист 61); мебель, текстиль и декор — по спецификации (лист 28). Образцы доски, керамогранита и тканей утвердить до заказа.
3. Фактуры на листе условные, цвет передан по HEX-значениям производителей: при печати возможны отклонения, решение — только по физическому образцу.

Изм.	Кол.уч	Лист	№ док.	Подп.	Дата
Разраб.		Кырлан А.С.			13.11.26
Пров.					
ГИП					
Н. контр.					
Утв.					

ГД-2026-011-АИ

Квартира 56 м²

ЖК «Северный парк», Москва

Дизайн-проект интерьера

Стадия	Лист	Листов
РП	26	119

Концепция интерьера

М б/м


Кырлан Александр Сергеевич

выпуск 13.11.2026 · eb78108141 · стр. 28 из 139

План расстановки мебели

Мебель и оборудование · размеры в мм от чистовых стен · марки — по ведомости

ПРЕДВАРИТЕЛЬНО · не для производства работ · открыто пунктов: 13 (реестр — л. 6, 7)

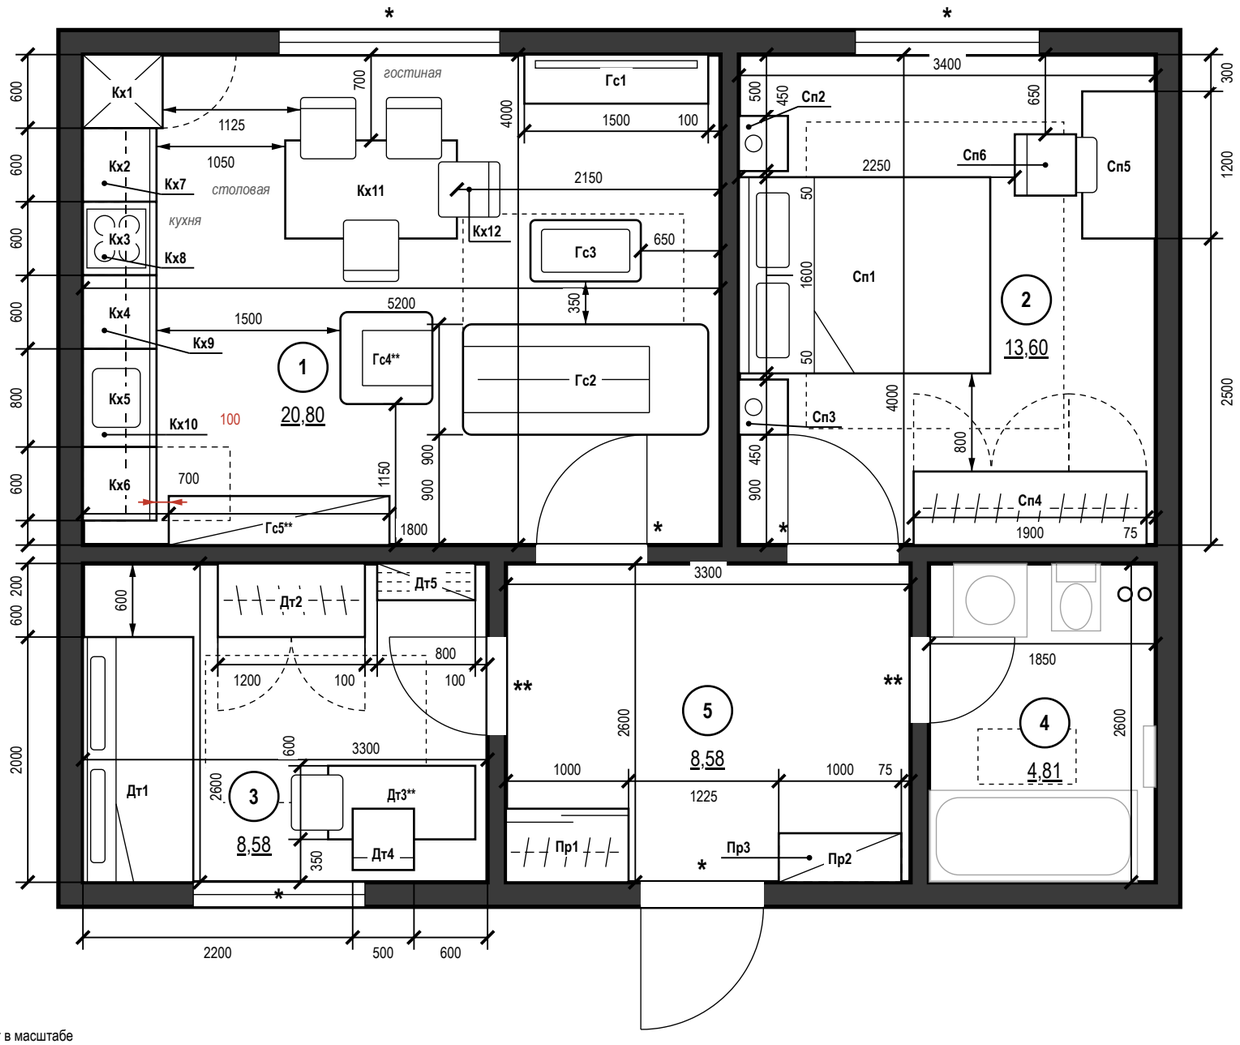
гостиная
столовая
кухня
Кх1
Кх2
Кх3
Кх4
Кх5
Кх6
Кх7
Кх8
Кх9
Кх10
Кх11
Кх12
Гс1
Гс2
Гс3
Гс4**
Гс5**
Сп1
Сп2
Сп3
Сп4
Сп5
Сп6
Дт1
Дт2
Дт3**
Дт4
Дт5
Пр1
Пр2
Пр3
1
20,80
2
13,60
3
8,58
4
4,81
5
8,58
3400
5200
3300
2250
1900
1850
1225
2200
2000
2600
2500
1200
1000
1800
2150
1500
1125
1050
700
4000
3300
1600
1200
1225
1900
1850

Спецификация мебели и оборудования

ПРЕДВАРИТЕЛЬНО · не для производства работ · открыто пунктов: 13 (реестр — л. 6, 7)

Форма 1 ГОСТ 21.110-2013 · позиции мебели — по плану расстановки

Поз.	Наименование и техническая характеристика	Тип, марка, обозначение документа, опросного листа	Код продукции	Поставщик	Ед. измерения	Кол.	Масса 1 ед., кг	Примечание
	Мебель встроенная и корпусная (изготовление по чертежам мебельщика)							
Кх1	Колонна с холодильником встроенным, фасад — дуб рифлёный; корпус ЛДСП 16 мм; фасады — МДФ 18 мм, эмаль матовая; цвет фасадов — в цвет стен (NCS S 0804-Y30R); Ш×Г×В 600×650×2350 мм	—	—	изготовление на заказ	шт.	1	—	пом. 1; крепление к стене
Кх2	Модуль с ящиками; корпус ЛДСП 16 мм; фасады — МДФ 18 мм, эмаль матовая; цвет фасадов — в цвет стен (NCS S 0804-Y30R); Ш×Г×В 600×600×900 мм	—	—	изготовление на заказ	шт.	1	—	пом. 1
Кх3	Модуль с варочной панелью и духовым шкафом; корпус ЛДСП 16 мм; фасады — МДФ 18 мм, эмаль матовая; цвет фасадов в цвет стен (NCS S 0804-Y30R); Ш×Г×В 600×600×900 мм	—	—	изготовление на заказ	шт.	1	—	пом. 1
Кх4	Модуль с ящиками; корпус ЛДСП 16 мм; фасады — МДФ 18 мм, эмаль матовая; цвет фасадов — в цвет стен (NCS S 0804-Y30R); Ш×Г×В 600×600×900 мм	—	—	изготовление на заказ	шт.	1	—	пом. 1
Кх5	Модуль под мойку; корпус ЛДСП 16 мм; фасады — МДФ 18 мм, эмаль матовая; цвет фасадов — в цвет стен (NCS S 0804-Y30R); Ш×Г×В 800×600×900 мм	—	—	изготовление на заказ	шт.	1	—	пом. 1
Кх6	Модуль под встраиваемую ПММ 60; без корпуса (ниша между соседними модулями); фасад на дверь машины — МДФ 18 мм, эмаль матовая; цоколь; цвет фасадов — в цвет стен (NCS S 0804-Y30R); Ш×Г×В 600×600×900 мм	—	—	изготовление на заказ	шт.	1	—	пом. 1
Кх7	Навесной шкаф, фасад — дуб рифлёный; корпус ЛДСП 16 мм; фасады — МДФ 18 мм, эмаль матовая; цвет фасадов — в цвет стен (NCS S 0804-Y30R); Ш×Г×В 600×350×900 мм	—	—	изготовление на заказ	шт.	1	—	пом. 1
Кх8	Вытяжка встроенная в навесной шкаф, рециркуляция до обмера вентканала; корпус ЛДСП 16 мм; фасады — МДФ 18 мм, эмаль матовая; цвет фасадов — в цвет стен (NCS S 0804-Y30R); Ш×Г×В 600×350×800 мм	—	—	изготовление на заказ	шт.	1	—	пом. 1
Кх9	Навесной шкаф; корпус ЛДСП 16 мм; фасады — МДФ 18 мм, эмаль матовая; цвет фасадов — в цвет стен (NCS S 0804-Y30R); Ш×Г×В 600×350×900 мм	—	—	изготовление на заказ	шт.	1	—	пом. 1
Кх10	Навесной шкаф 2 секции, с сушкой; корпус ЛДСП 16 мм; фасады — МДФ 18 мм, эмаль матовая; цвет фасадов — в цвет стен (NCS S 0804-Y30R); Ш×Г×В 1400×350×900 мм	—	—	изготовление на заказ	шт.	1	—	пом. 1
Сп4	Шкаф распашной 1900×600 до 2400, фасады — дуб рифлёный; корпус ЛДСП 16 мм; фасады — МДФ 18 мм, эмаль матовая; цвет фасадов — в цвет стен (NCS S 0804-Y30R); Ш×Г×В 1900×600×2400 мм	—	—	изготовление на заказ	шт.	1	—	пом. 2; крепление к стене
Дт2	Шкаф 1200×600 до 2200, фасады — дуб и серо-зелёный; корпус ЛДСП 16 мм; фасады — МДФ 18 мм, эмаль матовая; цвет фасадов — в цвет стен (NCS S 0804-Y30R); Ш×Г×В 1200×600×2200 мм	—	—	изготовление на заказ	шт.	1	—	пом. 3; крепление к стене
Пр1	Шкаф-купе 1000×600 до 2600, двери — дуб и зеркало; корпус ЛДСП 16 мм; фасады — ЛДСП 10 мм, декор «дуб натуральный» в профиле: алюминий, чёрный матовый; вставка — зеркало серебро 4 мм, плёнка безопасности; Ш×Г×В 1000×600×2510 мм	—	—	изготовление на заказ	шт.	1	—	пом. 5
Пр3	Антресоль над скамьёй 1000×400, фасад в цвет стены; каркас и полки — ЛДСП 16 мм, декор «дуб натуральный»; без фасадов; Ш×Г×В 1000×400×500 мм	—	—	изготовление на заказ	шт.	1	—	пом. 5; крепление к стене
	Мебель покупная							
Гс1	Тумба ТВ низкая, дуб, ТВ 55" шпон, дуб натуральный, матовое масло; Ш×Г×В 1500×400×450 мм	аналог: Ш×Г×В 1500×400×450 мм, шпон	—	аналог по характеристикам	шт.	1	—	пом. 1; замена ≤ габарита
Гс2	Диван низкий 2000×900, лён, сиденье 400; обивка — ткань, цвет Tikkurila X447; Ш×Г×В 900×2000×750 мм	аналог: Ш×Г×В 900×2000×750 мм, обивка — ткань	—	аналог по характеристикам	шт.	1	—	пом. 1; замена ≤ габарита

Примечания

1. Позиции мебели совпадают с марками на плане расстановки (лист 27); размеры Ш×Г×В — Ш вдоль стены, Г от стены.
2. Размеры и привязки плана расстановки — в мм от чистовых поверхностей стен: слой штукатурки 20 мм по блоку и 5 мм шпаклёвки по ГКЛ учтён; привязки — от стен и углов помещения, а не от другой мебели.
3. План расстановки не является документацией для изготовления мебели. Встроенная и корпусная мебель изготавливается по чертежам мебельщика после контрольного обмера (после штукатурки); «стена в стену» — с зазором 10 мм с каждой стороны или с компенсаторами; графы «Тип, марка» и «Код продукции» для неё не заполняются (ГОСТ 21.110-2013).
4. Покупные изделия — аналог по характеристикам: заменять только на изделия не больше указанного габарита и того же материала и цвета.
5. Материал и цвет, не указанные в данных изделия, приняты по концепции (лист 26): тон дерева — по полу, обивка — по вторичному цвету палитры; образцы согласовать до заказа.
6. Масса 1 ед. для изделий до 25 кг не указывается. Техника — по монтажным схемам изготовителя; выводы — по листам ЭОМ и ВК.

Допущения и предложения на листе

Основа листа: размеры помещений и положение проёмов введены заказчиком в брифе, на объекте не замерены (К-1); высота потолка 2700 мм — по брифу заказчика, не замерена (К-2); толщины стен приняты по брифу: наружные 200 мм, внутренние 150 мм — не обмерены (К-1); тип дома монолитный, перекрытие 200 мм — по брифу заказчика, документов нет (К-3); планировка (стены, проёмы, объединение кухни и гостиной, расширение санузла) — по брифу без обмера и плана БТИ (К-7); разрешённая мощность 10 кВт принята, ТУ не переданы (К-8); вентканалы приняты, в брифе не заданы (К-9); подрайон климата не задан — принят не северный (жилые от 2,5 м) (К-10).
См. лист открытых вопросов (лист 6, записи К-1–К-3, К-7–К-10).

Изм.	Кол.уч	Лист	№ док.	Подп.	Дата
Разраб.		Кырлан А.С.			13.11.26
Пров.					
ГИП					
Н. контр.					
Утв.					

ГД-2026-011-АИ

Квартира 56 м²

ЖК «Северный парк», Москва

Дизайн-проект интерьера

Стадия	Лист	Листов
РП	28	119

Спецификация мебели и оборудования

М б/м

Кырлан Александр Сергеевич

Спецификация мебели и оборудования (продолжение)

Форма 1 ГОСТ 21.110-2013 · позиции мебели — по плану расстановки

ПРЕДВАРИТЕЛЬНО · не для производства работ · открыто пунктов: 13 (реестр — л. 6, 7)

Поз.	Наименование и техническая характеристика	Тип, марка, обозначение документа, опросного листа	Код продукции	Поставщик	Ед. измерения	Кол.	Масса 1 ед., кг	Примечание
Гс3	Столик журнальный низкий, массив дуба; шпон, дуб натуральный, матовое масло; Ш×Г×В 900×500×350 мм	аналог: Ш×Г×В 900×500×350 мм, шпон	—	аналог по характеристикам	шт.	1	—	пом. 1; замена ≤ габарита
Гс4**	Кресло-лаунж, тёмный ясень и шерсть; обивка — ткань, цвет Tikkurila X447; Ш×Г×В 750×750×750 мм	аналог: Ш×Г×В 750×750×750 мм, обивка — ткань	—	аналог по характеристикам	шт.	1	—	пом. 1; замена ≤ габарита
Гс5**	Консоль низкая 1800×400, тёмный ясень, фасады рифлёные; шпон, дуб натуральный, матовое масло; Ш×Г×В 1800×400×700 мм	аналог: Ш×Г×В 1800×400×700 мм, шпон	—	аналог по характеристикам	шт.	1	—	пом. 1; крепление к стене; замена ≤ габарита
Кх11	Стол обеденный 1400×800, массив дуба, низкие стулья Wishbone; шпон, дуб натуральный, матовое масло; Ш×Г×В 1400×800×740 мм	аналог: Ш×Г×В 1400×800×740 мм, шпон	—	аналог по характеристикам	шт.	1	—	пом. 1; замена ≤ габарита
Кх12	Стул обеденный к столу Кх11; обивка — ткань, цвет Tikkurila X447; каркас — дуб натуральный; Ш×Г×В 450×500×820 мм	аналог: Ш×Г×В 450×500×820 мм, обивка — ткань	—	аналог по характеристикам	шт.	4	—	пом. 1; замена ≤ габарита
Сп1	Кровать-подиум 1600×2000, дуб, изголовье 900; мягкое изголовье, обивка — ткань, цвет Tikkurila X447; Ш×Г×В 1600×2050×900 мм	аналог: Ш×Г×В 1600×2050×900 мм, мягкое изголовье	—	аналог по характеристикам	шт.	1	—	пом. 2; замена ≤ габарита
Сп2, Сп3	Тумба прикроватная, дуб; шпон, дуб натуральный, матовое масло; Ш×Г×В 450×400×400 мм	аналог: Ш×Г×В 450×400×400 мм, шпон	—	аналог по характеристикам	шт.	2	—	пом. 2; замена ≤ габарита
Сп5	Стол рабочий у окна 1200×600, дуб (работа из дома); шпон, дуб натуральный, матовое масло; Ш×Г×В 1200×600×750 мм	аналог: Ш×Г×В 1200×600×750 мм, шпон	—	аналог по характеристикам	шт.	1	—	пом. 2; замена ≤ габарита
Сп6	Стул рабочий, гнутая фанера; обивка — ткань, цвет Tikkurila X447; каркас — дуб натуральный; Ш×Г×В 500×500×800 мм	аналог: Ш×Г×В 500×500×800 мм, обивка — ткань	—	аналог по характеристикам	шт.	1	—	пом. 2; замена ≤ габарита
Дт1	Кровать 900×2000 низкая, дуб, спинка-бортик 700 вдоль стены; мягкое изголовье, обивка — ткань, цвет Tikkurila X447; Ш×Г×В 2000×900×700 мм	аналог: Ш×Г×В 2000×900×700 мм, мягкое изголовье	—	аналог по характеристикам	шт.	1	—	пом. 3; замена ≤ габарита
Дт3**	Стол письменный растущий 1200×600; шпон, дуб натуральный, матовое масло; Ш×Г×В 600×1200×700 мм	аналог: Ш×Г×В 600×1200×700 мм, шпон	—	аналог по характеристикам	шт.	1	—	пом. 3; замена ≤ габарита
Дт4	Стул растущий; обивка — ткань, цвет Tikkurila X447; каркас — дуб натуральный; Ш×Г×В 500×500×800 мм	аналог: Ш×Г×В 500×500×800 мм, обивка — ткань	—	аналог по характеристикам	шт.	1	—	пом. 3; замена ≤ габарита
Дт5	Стеллаж низкий для книг и игрушек 800×300; шпон, дуб натуральный, матовое масло; Ш×Г×В 800×300×1200 мм	аналог: Ш×Г×В 800×300×1200 мм, шпон	—	аналог по характеристикам	шт.	1	—	пом. 3; крепление к стене; замена ≤ габарита
Пр2	Скамья-обувница 1000×400, дуб; Ш×Г×В 1000×400×450 мм	аналог: Ш×Г×В 1000×400×450 мм	—	аналог по характеристикам	шт.	1	—	пом. 5; замена ≤ габарита
	Техника встраиваемая и бытовая (покупные изделия), светильники под розетки							
	Холодильник встраиваемый, в модуле Кх1	аналог по характеристикам: полновстраиваемый под фасад, ниша 1780 × 560 × 550 мм, вентиляция решётка в цоколе, выход сверху	—	по выбору заказчика до изготовления мебели	шт.	1	—	пом. 1; по схеме изготовителя
	Посудомоечная машина встраиваемая, в модуле Кх6; ниша 600 мм	аналог по характеристикам: полновстраиваемая 60 см под фасад, ниша 600 × 862 мм, навеска фасада в комплекте	—	по выбору заказчика до изготовления мебели	шт.	1	—	пом. 1; по схеме изготовителя
	Вытяжка встраиваемая, в модуле Кх8	аналог по характеристикам: производительность — по расчёту ОВ, шум ≤ 55 дБ(А)	—	по выбору заказчика до изготовления мебели	шт.	1	—	пом. 1; по схеме изготовителя
	Варочная панель встраиваемая, индукционная, в модуле Кх3	аналог по характеристикам: индукционная 60 см, вырез 560 × 490 мм по шаблону модели	—	по выбору заказчика до изготовления мебели	шт.	1	—	пом. 1; по схеме изготовителя
	Духовой шкаф встраиваемый, в модуле Кх3	аналог по характеристикам: 60 см, лицевая панель 595 мм, ниша 560 × 600, глубина ≥ 550 мм, вентиляция за прибором	—	по выбору заказчика до изготовления мебели	шт.	1	—	пом. 1; по схеме изготовителя

Допущения и предложения на листе

Основа листа: размеры помещений и положение проёмов введены заказчиком в брифе, на объекте не замерены (К-1); высота потолка 2700 мм — по брифу заказчика, не замерена (К-2); толщины стен приняты по брифу: наружные 200 мм, внутренние 150 мм — не обмерены (К-1); тип дома монолитный, перекрытие 200 мм — по брифу заказчика, документов нет (К-3); планировка (стены, проёмы, объединение кухни и гостиной, расширение санузла) — по брифу без обмера и плана БТИ (К-7); разрешённая мощность 10 кВт принята, ТУ не переданы (К-8); вентканалы приняты, в брифе не заданы (К-9); подрайон климата не задан — принят не северный (жилые от 2,5 м) (К-10).

Знак «**» — предложение проектировщика, заказчиком не утверждено (согласовать с заказчиком): ИЗ-1: Гс4 — Было у 2300…3050; ИЗ-1–ИЗ-3: Дт3 — Было у стены В смещение 1000…2200 вплотную над радиатором РО-3 (900 мм под окном): прибор в корпусе, на развёртке — штрихом внутри стола; ИЗ-1, ИЗ-3: Гс5 — Было смещение 1600…3400 у двери Д-2 (3700…4600): между консолью и креслом/диваном оставался проход 575–625 мм, из двери к кухне не пройти.

См. лист открытых вопросов (лист 6, записи К-1–К-3, К-7–К-10; лист 7, записи ИЗ-1–ИЗ-3).

Изм.	Кол.уч	Лист	№ док.	Подп.	Дата
Разраб.		Кырлан А.С.			13.11.26
Пров.					
ГИП					
Н. контр.					
Утв.					

ГД-2026-011-АИ

Квартира 56 м²

ЖК «Северный парк», Москва

Дизайн-проект интерьера

Стадия	Лист	Листов
РП	29	119

Спецификация мебели и оборудования (продолжение)

М б/м

Кырлан Александр Сергеевич

выпуск 13.11.2026 № eb7810814f · стр. 31 из 139

Спецификация мебели и оборудования (продолжение)

Форма 1 ГОСТ 21.110-2013 · позиции мебели — по плану расстановки

ПРЕДВАРИТЕЛЬНО · не для производства работ · открыто пунктов: 13 (реестр — л. 6, 7)

Поз.	Наименование и техническая характеристика	Тип, марка, обозначение документа, опросного листа	Код продукции	Поставщик	Ед. измерения	Кол.	Масса 1 ед., кг	Примечание
	Стиральная машина, место по листу ВК (Сн4); Ш×Г 600×600 мм	аналог по характеристикам: тип загрузки — по листу ВК, в плане 600 × 600 мм (ширина × глубина), по листу ВК	—	по выбору заказчика до изготовления мебели	шт.	1	—	пом. 4; по схеме изготовителя
	Торшер, у поз. Гс2; абажур — ткань или опаловое стекло; лампа 2700 K	—	—	аналог по характеристикам	шт.	1	—	пом. 1; розетка Р21 (ЭОМ)
	Торшер, у поз. Сп3; абажур — ткань или опаловое стекло; лампа 2700 K	—	—	аналог по характеристикам	шт.	1	—	пом. 2; розетка Р5 (ЭОМ)
	Текстиль							
Т13	Портьеры-волна (гостиная); лён 70 %, вискоза 30 %; цвет Tikkurila X447; карниз 2250 мм, высота 2690 мм, сборка 2	—	—	аналог по характеристикам	шт.	2	—	пом. 1
Т14	Тюль (гостиная); полиэстер 100 %; цвет Tikkurila F485; карниз 2250 мм, высота 2690 мм, сборка 2,5	—	—	аналог по характеристикам	шт.	1	—	пом. 1
Т16	Ковёр в зоне отдыха, джут с шерстью; шерсть 100 %; цвет Tikkurila V484; 1800×1600 мм	—	—	аналог по характеристикам	шт.	1	—	пом. 1; с подложкой
Т17	Подушки на диван; букле (шерсть 60 %, полиэстер 40 %); цвет Tikkurila X447	—	—	аналог по характеристикам	шт.	2	—	пом. 1
Т18	Подушки на диван, акцент; хлопковый бархат 100 %; цвет Farrow & Ball No. 298	—	—	аналог по характеристикам	шт.	2	—	пом. 1
Т19	Плед на диван; альпака 50 %, шерсть 50 %; цвет Tikkurila V484	—	—	аналог по характеристикам	шт.	1	—	пом. 1
Т1	Портьеры-волна; лён 100 %; цвет Tikkurila X447; карниз 2500 мм, высота 2590 мм, сборка 2	—	—	аналог по характеристикам	шт.	2	—	пом. 2
Т2	Тюль; полиэстер 100 %; цвет Tikkurila F485; карниз 2500 мм, высота 2590 мм, сборка 2,5	—	—	аналог по характеристикам	шт.	1	—	пом. 2
Т3	Ковёр под кроватью, шерсть; шерсть 80 %, хлопок 20 %; цвет NCS S 2005-Y30R; 2100×2500 мм	—	—	аналог по характеристикам	шт.	1	—	пом. 2; с подложкой
Т4	Подушки декоративные на кровать; лён 100 %; цвет Tikkurila X447	—	—	аналог по характеристикам	шт.	2	—	пом. 2
Т5	Подушки на кровать, акцент; хлопковый бархат 100 %; цвет NCS S 5010-G70Y	—	—	аналог по характеристикам	шт.	2	—	пом. 2
Т6	Плед на кровать; шерсть мериноса 100 %; цвет NCS S 5010-G70Y	—	—	аналог по характеристикам	шт.	1	—	пом. 2
Т7	Портьеры-волна; лён 100 %; цвет Tikkurila X447; карниз 1820 мм, высота 2590 мм, сборка 2	—	—	аналог по характеристикам	шт.	2	—	пом. 3
Т8	Тюль; полиэстер 100 %; цвет Tikkurila F485; карниз 1820 мм, высота 2590 мм, сборка 2,5	—	—	аналог по характеристикам	шт.	1	—	пом. 3
Т9	Ковёр игровой, шерсть; шерсть 100 %; цвет Tikkurila V484; 1800×1200 мм	—	—	аналог по характеристикам	шт.	1	—	пом. 3; с подложкой
Т10	Подушки декоративные на кровать; букле (шерсть 60 %, полиэстер 40 %); цвет NCS S 1002-Y50R	—	—	аналог по характеристикам	шт.	2	—	пом. 3
Т11	Подушки на кровать, акцент; хлопковый бархат 100 %; цвет Tikkurila X447	—	—	аналог по характеристикам	шт.	2	—	пом. 3
Т12	Плед на кровать; шерсть мериноса 100 %; цвет Tikkurila X447	—	—	аналог по характеристикам	шт.	1	—	пом. 3
Т20**	Полотенца банные махровые, приглушённая олива, сложены на полотенцесушителе; хлопок 100 %; цвет NCS S 5010-G70Y	—	—	аналог по характеристикам	шт.	2	—	пом. 4
Т21**	Полотенца для рук вафельные, тёплый белый, на нижних перекладинах сушителя; хлопок 100 %; цвет Tikkurila F485	—	—	аналог по характеристикам	шт.	2	—	пом. 4
Т22**	Ковёр — коврик для ванной у бортика ванны, хлопок тафтинг, песочный; хлопок 100 %, латексная противоскользящая основа; цвет NCS S 2005-Y30R; 800×450 мм	—	—	аналог по характеристикам	шт.	1	—	пом. 4; с подложкой

Допущения и предложения на листе

Основа листа: размеры помещений и положение проёмов введены заказчиком в брифе, на объекте не замерены (К-1); высота потолка 2700 мм — по брифу заказчика, не замерена (К-2); толщины стен приняты по брифу: наружные 200 мм, внутренние 150 мм — не обмерены (К-1); тип дома монолитный, перекрытие 200 мм — по брифу заказчика, документов нет (К-3); планировка (стены, проёмы, объединение кухни и гостиной, расширение санузла) — по брифу без обмера и плана БТИ (К-7); разрешённая мощность 10 кВт принята, ТУ не переданы (К-8); вентканалы приняты, в брифе не заданы (К-9); подрайон климата не задан — принят не северный (жилые от 2,5 м) (К-10).

Знак «**» — предложение проектировщика, заказчиком не утверждено (согласовать с заказчиком): ИЗ-3: Т20, Т21, Т22.

См. лист открытых вопросов (лист 6, записи К-1–К-3, К-7–К-10; лист 7, запись ИЗ-3).

Изм.	Кол.уч	Лист	№ док.	Подп.	Дата
Разраб.		Кырлан А.С.			13.11.26
Пров.					
ГИП					
Н. контр.					
Утв.					

ГД-2026-011-АИ

Квартира 56 м²

ЖК «Северный парк», Москва

Дизайн-проект интерьера

Стадия	Лист	Листов
РП	30	119

Спецификация мебели и оборудования (продолжение)

М б/м

Кырлан Александр Сергеевич

Спецификация мебели и оборудования (продолжение)

Форма 1 ГОСТ 21.110-2013 · позиции мебели — по плану расстановки

ПРЕДВАРИТЕЛЬНО · не для производства работ · открыто пунктов: 13 (реестр — л. 6, 7)

Поз.	Наименование и техническая характеристика	Тип, марка, обозначение документа, опросного листа	Код продукции	Поставщик	Ед. измерения	Кол.	Масса 1 ед., кг	Примечание
	Декор							
ДК6	Картина над консолью: горный ручей, тушь суми-э, рама — тёмный ясень; 1000×700 мм; низ на 950 мм от пола	—	—	аналог по характеристикам	шт.	1	6	пом. 1; крепление: анкер, 2 шт.
ДК7	Фикус каучуконосный в кашпо Ø450, глина; 450×450 мм	—	—	аналог по характеристикам	шт.	1	—	пом. 1
ДК8	Ваза керамическая с одной веткой на обеденном столе; 200×350 мм; на Кх11	—	—	аналог по характеристикам	шт.	1	—	пом. 1
ДК11**	Книги стопкой и свеча в керамической чаше на журнальном столике; 300×130 мм; на Гс3	—	—	аналог по характеристикам	шт.	1	—	пом. 1
ДК12**	Вазы ручной работы разной высоты (340 и 220 мм), 2 шт., оливковая глазурь, на консоли Гс5**; 250×340 мм; на Гс5**	—	—	аналог по характеристикам	шт.	2	—	пом. 1
ДК13**	Лампа настольная на консоли Гс5**: основание — тёмный ясень, абажур — рисовая бумага; 220×480 мм; на Гс5**	—	—	аналог по характеристикам	шт.	1	—	пом. 1
ДК14**	Чаши ручной работы, 2 шт., и чайник, оливковая глазурь, на столешнице кухни; 280×220 мм; на Кх4	—	—	аналог по характеристикам	шт.	2	—	пом. 1
ДК1	Картина над кроватью: ветка сакуры, акварель, паспарту, рама — дуб; 1000×700 мм; низ на 1100 мм от пола	—	—	аналог по характеристикам	шт.	1	4	пом. 2; крепление к стене
ДС1**	Реечная панель: дуб, за изголовьем кровати; низ на 80 мм от пола	—	—	аналог по характеристикам	шт.	1	—	пом. 2
ДК15**	Книги стопкой на тумбе Сп2; 250×120 мм; на Сп2	—	—	аналог по характеристикам	шт.	1	—	пом. 2
ДК16**	Шеффлера в глиняном кашпо Ø350; 380×380 мм	—	—	аналог по характеристикам	шт.	1	—	пом. 2
ДК17**	Лампа настольная рабочая на столе Сп5: стойка — дуб, абажур-колпак — рисовая бумага; 220×480 мм; на Сп5	—	—	аналог по характеристикам	шт.	1	—	пом. 2
ДК3	Картина над кроватью: кот на подоконнике, детская иллюстрация, рама — светлый дуб; 1200×600 мм; низ на 900 мм от пола	—	—	аналог по характеристикам	шт.	1	4	пом. 3; крепление к стене
ДК4	Зеркало в рост в тонкой чёрной раме; рама — чёрный матовый; 500×1500 мм; низ на 300 мм от пола	—	—	аналог по характеристикам	шт.	1	12	пом. 3; крепление: анкер для пустотелых оснований, 4 шт.
ДК18**	Лампа настольная рабочая на столе Дт3**: шарнирная стойка — светлый дуб, абажур-колпак серо-зелёный; 220×480 мм; на Дт3**	—	—	аналог по характеристикам	шт.	1	—	пом. 3
ДК2	Зеркало над умывальником, влагостойкое, с подсветкой; 600×800 мм; низ на 1200 мм от пола	—	—	аналог по характеристикам	шт.	1	—	пом. 4
ДК9**	Ваза-бутыль керамическая, приглушённая олива, с сухой веткой эвкалипта — на полке короба инсталляции; 130×400 мм	—	—	аналог по характеристикам	шт.	1	—	пом. 4
ДК5	Зеркало над скамьёй, тонкая чёрная рама; рама — чёрный матовый; 600×1200 мм; низ на 700 мм от пола	—	—	аналог по характеристикам	шт.	1	18	пом. 5; крепление: анкер, 4 шт.
ДК10**	Графика в раме из тёмного ясеня 400×560: энсо — круг одним движением кисти, тушь; 400×560 мм; низ на 1220 мм от пола	—	—	аналог по характеристикам	шт.	1	2	пом. 5; крепление: дюбель с крюком, 2 точки

Допущения и предложения на листе

Основа листа: размеры помещений и положение проёмов введены заказчиком в брифе, на объекте не замерены (К-1); высота потолка 2700 мм — по брифу заказчика, не замерена (К-2); толщины стен приняты по брифу: наружные 200 мм, внутренние 150 мм — не обмерены (К-1); тип дома монолитный, перекрытие 200 мм — по брифу заказчика, документов нет (К-3); планировка (стены, проёмы, объединение кухни и гостиной, расширение санузла) — по брифу без обмера и плана БТИ (К-7); разрешённая мощность 10 кВт принята, ТУ не переданы (К-8); вентканалы приняты, в брифе не заданы (К-9); подрайон климата не задан — принят не северный (жилые от 2,5 м) (К-10).

Знак «**» — предложение проектировщика, заказчиком не утверждено (согласовать с заказчиком): ДС1 — реечная панель из дуба за изголовьем — предложение исполнителя по стилю джапанди (бриф: натуральное дерево), заказчиком не утверждена; ИЗ-1–ИЗ-3: Дт3 — Было у стены В смещение 1000…2200 вплотную над радиатором РО-3 (900 мм под окном): прибор в корпусе, на развёртке — штрихом внутри стола; ИЗ-1, ИЗ-3: Гс5 — Было смещение 1600…3400 у двери Д-2 (3700…4600): между консолью и креслом/диваном оставался проход 575–625 мм, из двери к кухне не пройти; ИЗ-3: ДК11, ДК12, ДК13, ДК14, ДК15, ДК16, ДК17, ДК18, ДК9, ДК10.

См. лист открытых вопросов (лист 6, записи К-1–К-3, К-7–К-10; лист 7, записи ИЗ-1–ИЗ-3).

Изм.	Кол.уч	Лист	№ док.	Подп.	Дата
Разраб.		Кырлан А.С.			13.11.26
Пров.					
ГИП					
Н. контр.					
Утв.					

ГД-2026-011-АИ

Квартира 56 м²

ЖК «Северный парк», Москва

Дизайн-проект интерьера

Стадия	Лист	Листов
РП	31	119

Спецификация мебели и оборудования (продолжение)

М б/м

Кырлан Александр Сергеевич

выпуск 13.11.2026 № eb7810814f · стр. 33 из 139

03


Электрооборудование

Кырлан Александр Сергеевич

План розеток и электровыводов

Розетки, выводы кабеля, щит · размеры в мм · высоты от чистого пола

План розеток (М 1:50)

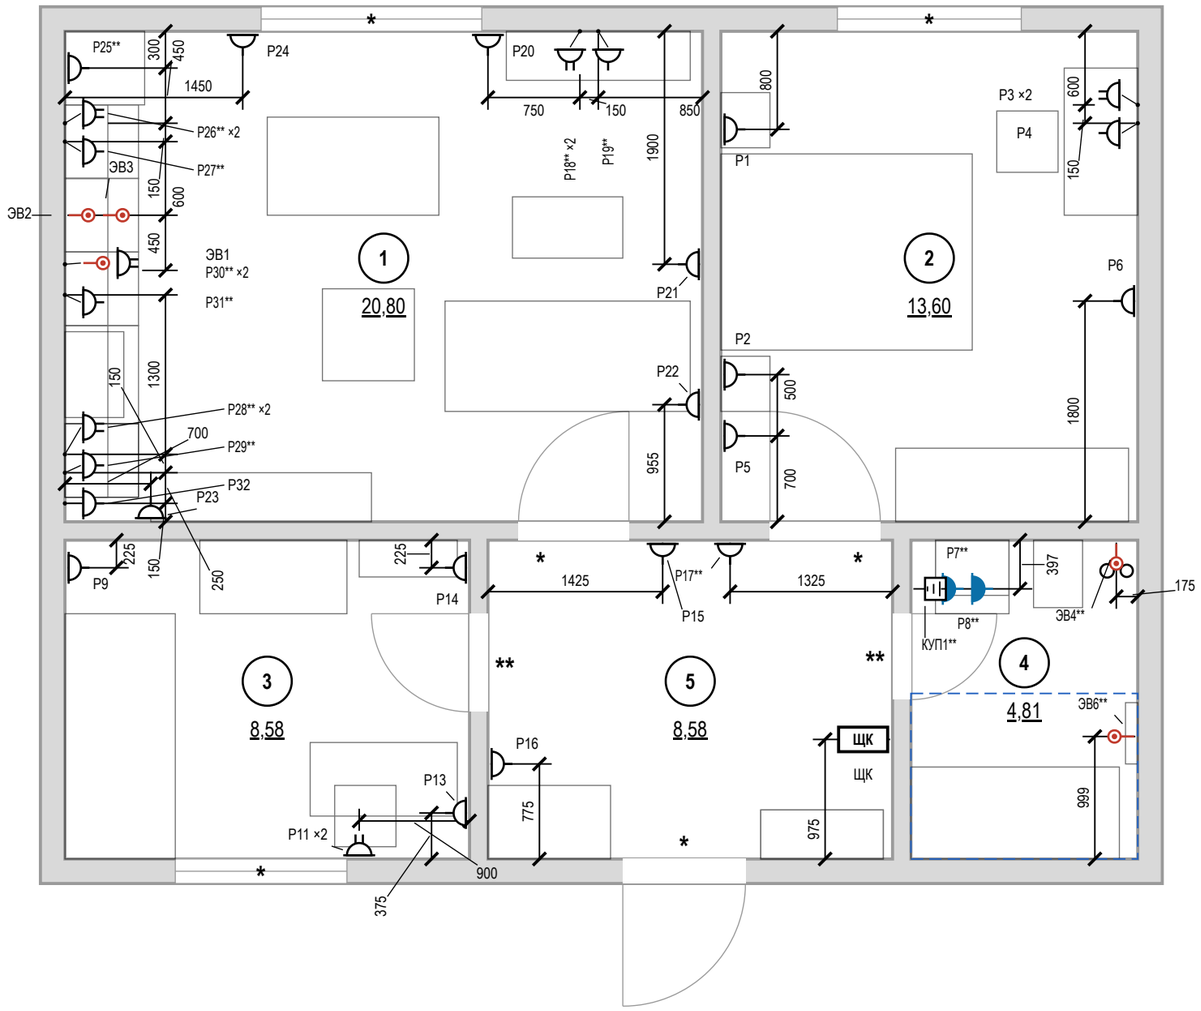

Допущения и предложения на листе. Основа листа: размеры помещений и положение проёмов введены заказчиком в брифе, не замерены (К-1); высота потолка 2700 мм — по брифу заказчика, не замерена (К-2); толщины стен приняты по брифу: наружные 200 мм, внутренние 150 мм — не обмерены (К-1); тип дома монолитный, перекрытие 200 мм — по брифу заказчика, документов нет (К-3); планировка (стены, проёмы, объединение кухни и гостиной, расширение санузла) — по брифу без обмера и плана БТИ (К-7); разрешённая мощность 10 кВт принята, ТУ не переданы (К-8); вентканалы приняты, в брифе не заданы (К-9); подрайон климата не задан — принят не северный (жилые от 2,5 м) (К-10). Знак «*» — принято, не замерено (замерить): К-4: Ст К1-1, Ст В1-1. Знак «**» — предложено, не утверждено (согласовать): Р18, Р19, Р25, Р26, Р27, Р28, Р29, Р30, Р31, Р7, Р8, ЭВ4, КУП1, ЭВ6, Р17. См. лист открытых вопросов (лист 6, записи К-1–К-5, К-7–К-10).

Примечания

1. За отметку 0,000 принят уровень чистого пола. Высоты Н — от чистого пола до оси изделия; привязки — от чистовой грани стены до оси механизма (у рамки на несколько постов — до оси рамки).
2. Высоты Н и группы щита — в ведомости электроточек: розетки — 300 мм от чистого пола до оси механизма, если в ведомости не указано иное; выводы кабеля — по паспорту прибора.
3. Розетки в санузле — только вне зон 0–2 (ПУЭ 7.1.48, ГОСТ Р 50571.7.701-2024), IP44, через УЗО 30 мА.
4. Розеточные и мокрые линии — через УЗО или дифавтомат с током утечки не более 30 мА (ПУЭ 7.1.79); в санузле выполнить ДСУП (ПУЭ 7.1.87–7.1.88).
5. Кабель — медный, исполнение нг(А)-LS (ГОСТ 31565-2012); скрытая прокладка только горизонтально и вертикально, фактические трассы зафиксировать исполнительной схемой до закрытия отделкой.
6. Расчёт нагрузок, токов КЗ, селективности и сечений — по проекту ЭОМ организации с допуском СРО; лист задаёт состав, расположение и группы.
7. Выводы кухонной техники — после утверждения проекта кухни (ориентировочно); привязки выводов даны от осей модулей гарнитура и пересматриваются вместе с проектом кухни.
8. Электрический тёплый пол проектом не предусмотрен; при решении заказчика устроить — отдельный лист «План тёплых полов»: контуры с отступом 100 мм от стен и мебели без ножек, датчик в гофре, терморегулятор, своя группа щита через УЗО 30 мА.
9. Ведомости электроточек, изделий, светильников и расшифровка клавиш — лист 35.

1000 мм · печать 1:1

ПРЕДВАРИТЕЛЬНО · не для производства работ · открыто пунктов: 13 (реестр — л. 6, 7)

Условные обозначения

Знак	Тип изделия	Н, мм	Кол., шт
	Розетка с заземлением	300	12
	То же	у знака	10
	Блок розеток с заземлением, рамка 2 поста	300	1
	То же	у знака	5
	Розетка с заземлением IP44	у знака	2
	Вывод кабеля к прибору	у знака	5
	КУП (уравнивание потенциалов)	300	1
ЩК	Щит квартирный	1700	1

розетка с заземляющим контактом; у знака — марка и ×N — число постов в рамке; группа щита, высота оси и назначение — в ведомости точек

знак разведён для читаемости: точка на стене — у выноски, привязка — до неё

граница зоны 2 ванной (600 мм от ванны/поддона)

мебель и сантехприборы — подложка

стояк: К1 — канализация, В1 — ХВС, Т3 — ГВС

1 — номер помещения, площадь м²

Итого розеток (механизмов) — 36 шт; рамок — 30 шт: на 1 пост — 24, на 2 поста — 6.


Изм.	Кол.уч	Лист	№ док.	Подп.	Дата			
Разраб.		Кырлан А.С.			13.11.26	**ГД-2026-011-АИ**		
Пров.						Квартира 56 м² ЖК «Северный парк», Москва		
ГИП						Дизайн-проект интерьера	Стадия: РП	Лист: 32 / Листов: 119
Н. контр.						**План розеток и электровыводов** М 1:50	**Кырлан Александр Сергеевич**	
Утв.								

выпуск 13.11.2026 № eb7810814f · стр. 35 из 139

План освещения

Светильники, группы включения, извещатели · размеры в мм

План освещения (М 1:50)

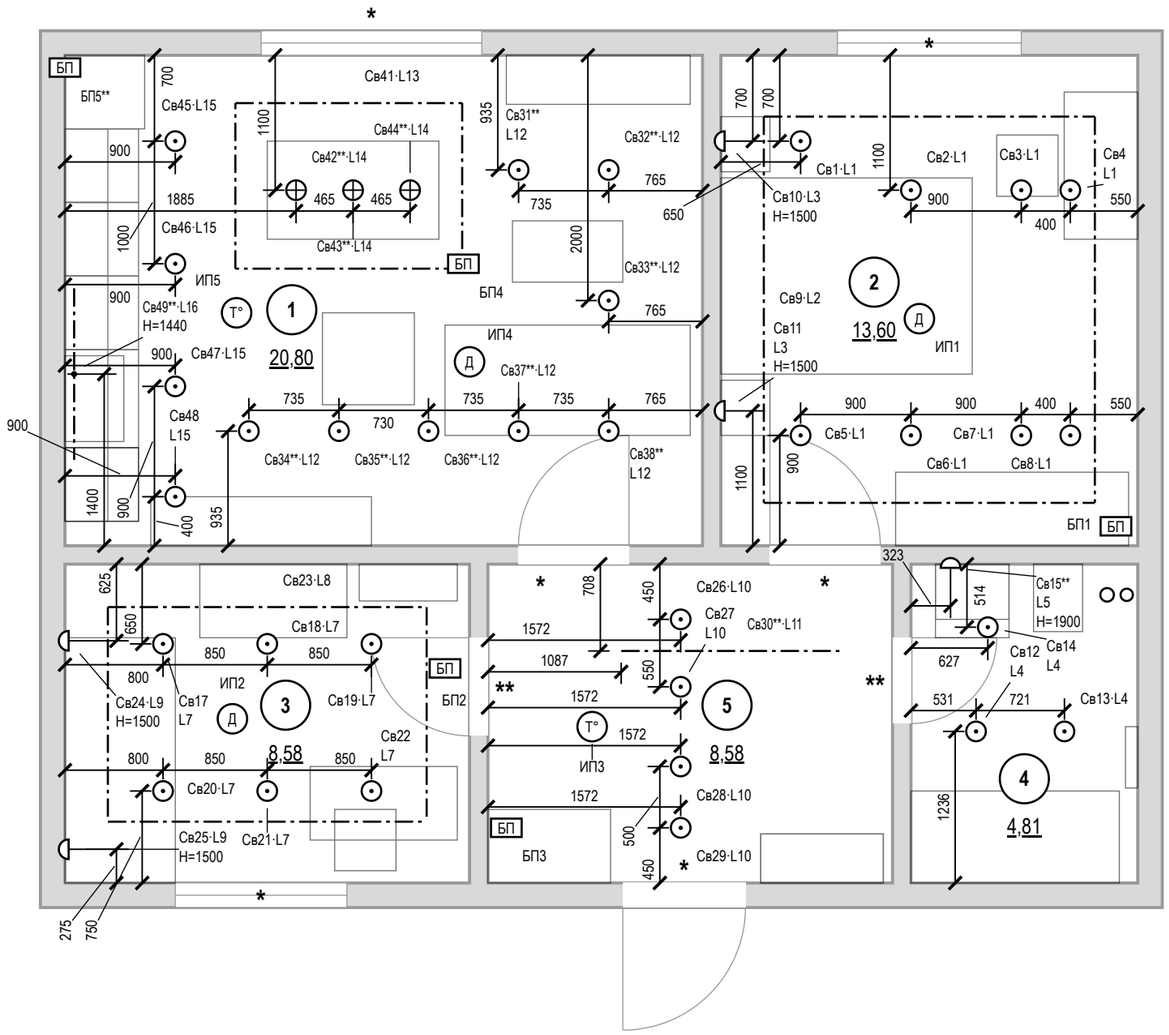

Условные обозначения

- светильник встраиваемый точечный
- светильник подвесной
- светильник настенный (бра), H — высота оси
- линейный светильник настенный (подсветка столешницы), точка — вывод питания
- светодиодная лента в профиле / в карнизе короба
- Св1·L1 — марка светильника (как в ведомости и на развёртках) · группа включения L (лист 34)
- Д — извещатель пожарный дымовой автономный
- Т° — извещатель пожарный тепловой
- БП — блок питания LED, с доступом (люк от 100×100 мм)
- мебель и сантехприборы — подложка
- стояк: К1 — канализация, В1 — ХВС, Т3 — ГВС
- 1 — номер помещения, площадь м²

Допущения и предложения на листе

Основа листа: размеры помещений и положение проёмов введены заказчиком в брифе, на объекте не замерены (К-1); высота потолка 2700 мм — по брифу заказчика, не замерена (К-2); толщины стен приняты по брифу: наружные 200 мм, внутренние 150 мм — не обмерены (К-1); тип дома монолитный, перекрытие 200 мм — по брифу заказчика, документов нет (К-3); планировка (стены, проёмы, объединение кухни и гостиной, расширение санузла) — по брифу без обмера и плана БТИ (К-7); разрешённая мощность 10 кВт принята, ТУ не переданы (К-8); вентканалы приняты, в брифе не заданы (К-9); подрайон климата не задан — принят не северный (жилые от 2,5 м) (К-10).

Знак «*» — принято, не замерено и не подтверждено (замерить на объекте): К-1: окно пом. 1 (стена А) — окно: положение, ширина, высота и подоконник — по брифу заказчика, не замерены; ограждение 900 мм — предложение исполнителя; дверь пом. 1 (стена В) — Петли у правого откоса (х 4600): открытое полотно стоит у стены Б, вошедший идёт влево к кухне; при петлях слева полотно запирало вход в карман между собой, диваном Гс2 и стеной Б; окно пом. 2 (стена А), 3 (В) — окно: положение, ширина, высота и подоконник — по брифу заказчика, не замерены; дверь пом. 2 (стена В) — проём в существующей стене между пом. 2 и 5: положение и ширина — по брифу заказчика, не замерены; дверь пом. 5 (стена В) — входная дверь: положение и ширина проёма — по брифу заказчика, не замерены; К-4: Ст К1-1 — положение стояка канализации — по брифу заказчика, не замерено; Ст В1-1 — положение стояка холодной воды — по брифу заказчика, не замерено.

Знак «**» — предложение проектировщика, заказчиком не утверждено (согласовать с заказчиком): Св31, Св32, Св33, Св34, Св35, Св36, Св37, Св38 — ряды — по зоне гостиной (по мебели); Св42, Св43, Св44, Св49, БП5 — диммируемость добавлена разработчиком проекта под светорегуляторы S8 и S9; Св15 — Сдвиг под раскладку плитки стены А на 52 мм вдоль стены — ось на шве или в центре плитки, привязка по таблице листа; Св30 — открытая лента в накладном профиле вместо «в коробе»: короба в потолке нет — подвесной потолок помещения без короба и ниши LED; К-5: дверь пом. 3 (стена Б), 4 (Г) — дверь в новой перегородке: проём по брифу, короб скрытой двери и размер в свету — после выбора модели и утверждения перегородки (К-5).

См. лист открытых вопросов (лист 6, записи К-1–К-5, К-7–К-10).

Примечания

1. За отметку 0,000 принят уровень чистого пола. Высоты H — от чистого пола до оси изделия; привязки — от чистовой грани стены до оси механизма (у рамки на несколько постов — до оси рамки).
2. Высота установки, не указанная на плане: светильники — на потолке; настенные — по отметке H у знака. Привязки — до оси светильника от чистовой грани стены, по рядам.
3. Во влажных помещениях — светильники не ниже IP44; в зонах 0–2 ванной — по ГОСТ Р 50571.7.701-2024 (зона 1 — IPX5).
4. LED-лента в карнизе подсветки короба — по линии карниза с плана потолков; блок питания — в люке короба (БП на плане), питание ленты длиннее 5 м — с двух концов.
5. Розеточные и мокрые линии — через УЗО или дифавтомат с током утечки не более 30 мА (ПУЭ 7.1.79); в санузле выполнить ДСУП (ПУЭ 7.1.87–7.1.88).
6. Кабель — медный, исполнение нг(А)-LS (ГОСТ 31565-2012); скрытая прокладка только горизонтально и вертикально, фактические трассы зафиксировать исполнительной схемой до закрытия отделкой.
7. Расчёт нагрузок, токов КЗ, селективности и сечений — по проекту ЭОМ организации с допуском СРО; лист задаёт состав, расположение и группы.
8. Ведомость светильников (тип, количество, мощность, поток, Tц, Ra) — лист 51.
9. Оценка освещённости (по норме СанПиН 1.2.3685-21, табл. 5.52, на полу; не светотехнический расчёт, декоративная подсветка в оценку не входит) — лист 35.

1000 мм · печать 1:1

Изм.	Кол.уч	Лист	№ док.	Подп.	Дата
Разраб.		Кырлан А.С.			13.11.26
Пров.					
ГИП					
Н. контр.					
Утв.					

ГД-2026-011-АИ

Квартира 56 м²

ЖК «Северный парк», Москва

Дизайн-проект интерьера

Стадия	Лист	Листов
РП	33	119

План освещения

М 1:50

Кырлан Александр Сергеевич

ПРЕДВАРИТЕЛЬНО · не для производства работ · открыто пунктов: 13 (реестр — л. 6, 7)


выпуск 13.11.2026 № eb7810814f · стр. 36 из 139

План выключателей и схема включения

Выключатели S, группы включения L, линии связи · размеры в мм

ПРЕДВАРИТЕЛЬНО · не для производства работ · открыто пунктов: 13 (реестр — л. 6, 7)

План выключателей (М 1:50)

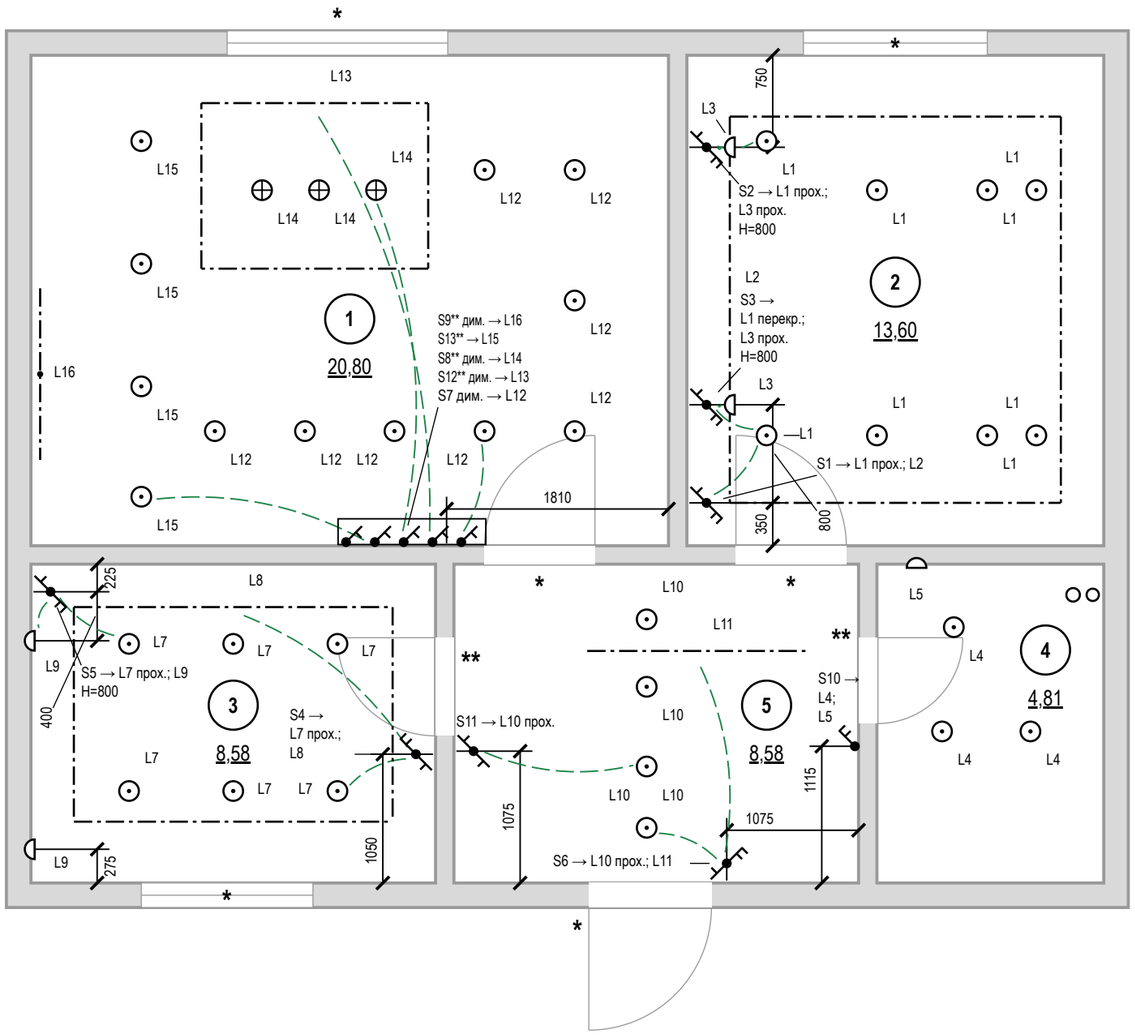

Условные обозначения

- выключатель одноклавишный
- выключатель двухклавишный (флажков — по числу клавиш)
- выключатель с проходной или перекрёстной клавишей (обратный флажок); тип клавиши — в подписи
- S1 → — марка → группы по клавишам (через «;»): прох. — проходной, перекр. — перекрёстный, дим. — светорегулятор; Н — высота
- связь: выключатель → ближайший светильник группы в том же помещении (не трасса кабеля); полный состав группы — по номеру L
- светильник встраиваемый точечный
- светильник подвесной
- светильник настенный (бра), Н — высота оси
- линейный светильник настенный (подсветка столешницы), точка — вывод питания
- светодиодная лента в профиле / в карнизе короба
- L1 — группа включения у светильника
- стояк: К1 — канализация, В1 — ХВС, Т3 — ГВС
- 1 — номер помещения, площадь м²

Допущения и предложения на листе

Основа листа: размеры помещений и положение проёмов введены заказчиком в брифе, на объекте не замерены (К-1); высота потолка 2700 мм — по брифу заказчика, не замерена (К-2); толщины стен приняты по брифу: наружные 200 мм, внутренние 150 мм — не обмерены (К-1); тип дома монолитный, перекрытие 200 мм — по брифу заказчика, документов нет (К-3); планировка (стены, проёмы, объединение кухни и гостиной, расширение санузла) — по брифу без обмера и плана БТИ (К-7); разрешённая мощность 10 кВт принята, ТУ не переданы (К-8); вентканалы приняты, в брифе не заданы (К-9); подрайон климата не задан — принят не северный (жилые от 2,5 м) (К-10).

Знак «*» — принято, не замерено и не подтверждено (замерить на объекте): К-1: окно пом. 1 (стена А) — окно: положение, ширина, высота и подоконник — по брифу заказчика, не замерены; ограждение 900 мм — предложение исполнителя; дверь пом. 1 (стена В) — Петли у правого откоса (х 4600): открытое полотно стоит у стены Б, вошедший идёт влево к кухне; при петлях слева полотно запирало вход в карман между собой, диваном Гс2 и стеной Б; окно пом. 2 (стена А), 3 (В) — окно: положение, ширина, высота и подоконник — по брифу заказчика, не замерены; дверь пом. 2 (стена В) — проём в существующей стене между пом. 2 и 5: положение и ширина — по брифу заказчика, не замерены; дверь пом. 5 (стена В) — входная дверь: положение и ширина проёма — по брифу заказчика, не замерены; К-4: Ст К1-1 — положение стояка канализации — по брифу заказчика, не замерено; Ст В1-1 — положение стояка холодной воды — по брифу заказчика, не замерено.

Знак «**» — предложение проектировщика, заказчиком не утверждено (согласовать с заказчиком): S12 — свой пост группе L13: сценарии «Вечер», «Ужин», «Кино», «Готовка» включают её отдельно от L12 — на одном светорегуляторе не набрать; S8, S9 — светорегулятор добавлен разработчиком проекта; S13 — свой пост группе L15: сценарии «Вечер», «Ужин», «Готовка» включают её отдельно от L14 — на одном светорегуляторе не набрать; К-5: дверь пом. 3 (стена Б), 4 (Г) — дверь в новой перегородке: проём по брифу, короб скрытой двери и размер в свету — после выбора модели и утверждения перегородки (К-5).

Открытые вопросы и конфликты по листу: К-12.

См. лист открытых вопросов (лист 6, записи К-1–К-5, К-7–К-10; лист 7, запись К-12).

Примечания

1. За отметку 0,000 принят уровень чистого пола. Высоты Н — от чистого пола до оси изделия; привязки — от чистовой грани стены до оси механизма (у рамки на несколько постов — до оси рамки).
2. Высота установки, не указанная на плане: выключатели — 900 мм от чистого пола (у кровати и другие — Н у марки), со стороны дверной ручки (ПУЭ 7.1.51).
3. Какой выключатель какие светильники включает — по номеру группы L: у выключателя (S1 → L1; L2 — клавиши по порядку) и у каждого светильника. Пунктир подсказка к ближайшему светильнику группы в том же помещении (не дальше 3 м), это не трасса кабеля; выключатель за стеной (у двери санузла) и далёкая группа — только номер группы.
4. Группы из нескольких мест (L1 — S1, S2, S3; L3 — S2, S3; L7 — S4, S5; L10 — S6, S11): на крайних местах — проходные клавиши, на промежуточных — перекрёстные; механизмы — в ведомости изделий.
5. Светорегулятор — по заднему фронту (для LED-драйверов), совместимость с драйверами проверить до закупки.
6. Розеточные и мокрые линии — через УЗО или дифавтомат с током утечки не более 30 мА (ПУЭ 7.1.79); в санузле выполнить ДСУП (ПУЭ 7.1.87–7.1.88).
7. Кабель — медный, исполнение нг(А)-LS (ГОСТ 31565-2012); скрытая прокладка только горизонтально и вертикально, фактические трассы зафиксировать исполнительной схемой до закрытия отделкой.
8. Расчёт нагрузок, токов КЗ, селективности и сечений — по проекту ЭОМ организации с допуском СРО; лист задаёт состав, расположение и группы.
9. Расшифровка клавиш и ведомость изделий — лист 35.

1000 мм · печать 1:1

Изм.	Кол.уч	Лист	№ док.	Подп.	Дата	ГД-2026-011-АИ			
						Квартира 56 м²			
						ЖК «Северный парк», Москва			
Разраб.		Кырлан А.С.			13.11.26	Дизайн-проект интерьера	Стадия	Лист	Листов
Пров.							РП	34	119
ГИП						План выключателей и схема включения	Кырлан Александр Сергеевич		
Н. контр.						М 1:50			
Утв.									

выпуск 13.11.2026 № eb7810814f · стр. 37 из 139

Ведомость электроточек и изделий

Электроточки, изделия, светильники, освещённость, клавиши выключателей · б/м

Ведомость электроточек

Марка	Пом.	Назначение	Н, мм	Гр.
Р18**	1	ТВ (в одной зоне с ТВ1, LAN3)	1100	6
Р19**	1	ТВ-приставка (в одной зоне с ТВ1, LAN3)	1100	6
Р20	1	у ТВ-тумбы	300	6
Р21	1	торшер	300	6
Р22	1	у дивана	300	6
Р23	1	уборка, пылесос	300	6
Р24	1	у обеденного стола	300	6
Р25**	1	холодильник — над нишей, съёмная панель	2120	11
Р26**	1	фартук	1175	7
Р27**	1	фартук	1175	7
Р28**	1	фартук	1175	7
Р29**	1	фартук	1175	7
Р30**	1	фартук между мойкой и варочной	1175	7
Р31**	1	фартук между мойкой и варочной	1175	7
Р32	1	посудомоечная машина (на стене за торцом гарнитура, доступ сбоку)	300	10
ЭВ1	1	варочная панель — в соседнем модуле, за ящиком	600	8
ЭВ2	1	духовой шкаф	150	9
ЭВ3	1	вытяжка — над корпусом	2200	11
Р1	2	у кровати	600	4
Р2	2	у кровати	600	4
Р3	2	рабочий стол	900	4
Р4	2	рабочий стол	900	4
Р5	2	торшер	300	4
Р6	2	уборка	300	4
Р9	3	у кровати	600	5
Р11	3	рабочий стол	300	5
Р13	3	уборка	300	5
Р14	3	уборка у входа	300	5
КУП1**	4	КУП — уравнивание потенциалов (ДСУП)	300	
Р7**	4	стиральная машина, IP44	1000	12

Ведомость электроточек (продолжение)

Марка	Пом.	Назначение	Н, мм	Гр.
Р8**	4	фен у умывальника, IP44	1141	13
ЭВ4**	4	вентилятор ВР1 (таймер выбега)	2450	3
ЭВ6**	4	полотенцесушитель Сн5, IP44	700	13
Р15	5	пылесос, сушилка обуви	300	6
Р16	5	уборка	300	6
Р17**	5	питание слаботочного щита (рядом с ЩС**)	1700	14
ЩК	5	щит квартирный ЩРВ-П-48	1700	

Ведомость изделий

Наименование	Марки	Ед.	Кол.
Розетка с з/к и защитными шторками, 16 А	по ведомости точек	шт	34
Розетка IP44 с крышкой, 16 А	Р7**, Р8**	шт	2
Выключатель 1-клав.	S13**	шт	1
Выключатель 1-клав. проходной	S11	шт	1
Выключатель 2-клав.	S10	шт	1
Выключатель 2-клав. (перекрёстная + проходная)	S3	шт	1
Выключатель 2-клав. (проходная + обычная)	S1, S4–S6	шт	4
Выключатель 2-клав. проходной	S2	шт	1
Светорегулятор 1-канальный, задний фронт (LED)	S7, S8**, S9**, S12**	шт	4
Датчик движения ночной подсветки	L11	шт	1
Рамка 1-постовая	в т. ч. 13 под выключ.	шт	37
Рамка 2-постовая		шт	6
Коробка установочная (подрозетник) Ø68	розетки, выключатели	шт	49
Вывод кабеля под прибор (клеммник)	ЭВ1–ЭВ3, ЭВ4**, ЭВ6**	шт	5
Коробка уравнивания потенциалов КУП	КУП1**	шт	1
Блок питания LED 24 В, 300 Вт, дим.	БП4	шт	1
Блок питания LED 24 В, 60 Вт, дим.	БП5**	шт	1
Блок питания LED 24 В, 200 Вт, дим.	БП1, БП2	шт	2
Блок питания LED 24 В, 20 Вт	БП3	шт	1
Извещатель дымовой автономный	ИП1, ИП2, ИП4	шт	3

Ведомость изделий (продолжение)

Наименование	Марки	Ед.	Кол.
Извещатель тепловой	ИП3, ИП5	шт	2
Щит квартирный (состав — лист щита)	ЩК	шт	1
Розетка компьютерная RJ45, кат. 6, с рамкой и подрозетником	LAN1–LAN3	шт	3
Розетка телевизионная (коаксиальная) с рамкой и подрозетником	ТВ1	шт	1
Точка доступа Wi-Fi (оборудование заказчика), питание PoE	АР1**, АР2**	шт	2
Трубка или монитор домофона (поставка домофонной организации)	ДФ1	шт	1
Щит слаботочный ЩС**: корпус, DIN-рейка, розетки 220 В	ЩС**	шт	1
Патч-панель, портов не менее 5		шт	1
Коммутатор, портов не менее 5, из них PoE 2		шт	1
Кабель домофона — тип по системе поставщика (по лучам от ЩС**, запас 10 %)		м	6,7
Кабель коаксиальный RG-6 (75 Ом) к розеткам ТВ (по лучам от ЩС**, запас 10 %)		м	11,7
Кабель U/UTP кат. 6 (LAN, Wi-Fi и камеры по PoE) (по лучам от ЩС**, запас 10 %)		м	44,9

Ведомость светильников

Поз.	Марки	Тип	Кол.	Р, Вт	Ф, лм	IP	Тц/Ra
1	Св31**, Св32**, Св33**, Св34**, Св35**, Св36**, Св37**, Св38**	встраиваемый точечный	8	12	1000		3000/90
2	Св41	светодиодная лента, 6,4 м	1	61,4	5760		2700/90
3	Св42**, Св43**, Св44**	подвесной	3	9	800		3000/90
4	Св45–Св48	встраиваемый точечный	4	10	900		3000/90
5	Св49**	линейный светильник, Н=1440	1	18	1500		3000/90
6	Св1–Св8	встраиваемый точечный	8	12	1000		2700/90
7	Св9	светодиодная лента, 11,7 м	1	112,3	10530		2700/90

Ведомость светильников (продолжение)

Поз.	Марки	Тип	Кол.	Р, Вт	Ф, лм	IP	Тц/Ra
8	Св10, Св11, Св24, Св25	настенный (бра), Н=1500	4	6	400		2700/90
9	Св17–Св22	встраиваемый точечный	6	12	1050		2700/90
10	Св23	светодиодная лента, 8,7 м	1	83,5	7830		2700/90
11	Св12–Св14	встраиваемый точечный	3	6	500	44	3000/90
12	Св15**	настенный (бра), Н=1900	1	8	600	44	3000/90
13	Св26–Св29	встраиваемый точечный	4	7	600		3000/90
14	Св30**	светодиодная лента, 1,8 м	1	8,6	270		2700/90

Освещённость (оценка)

Пом.	S, м²	Ен, лк	Ф треб., лм	Ф по пр., лм
1	20,8	150	8790	14000
2	13,6	150	5750	8000
3	8,6	200	4830	6300
4	4,8	50	680	1500
5	8,6	50	1210	2400

Расшифровка клавиш

Марка	Пом.	Н, мм	Клав.	Механизм	Группа: светильники
S1	2	900	1	проходной	L1: Св1–Св8
			2	обычный	L2: Св9
S2	2	800	1	проходной	L1: Св1–Св8
			2	проходной	L3: Св10, Св11
S3	2	800	1	перекрёстный	L1: Св1–Св8
			2	проходной	L3: Св10, Св11
S4	3	900	1	проходной	L7: Св17–Св22
			2	обычный	L8: Св23
S5	3	800	1	проходной	L7: Св17–Св22
			2	обычный	L9: Св24, Св25
S6	5	900	1	проходной	L10: Св26–Св29
			2	обычный	L11: Св30**

Примечания

1. Ведомости сведены с планов розеток, освещения и выключателей; марки, группы и высоты — те же, что у знаков на планах.
2. Механизмы, рамки и светорегуляторы — одной серии; число постов и клавиш сверено с выбранной серией. Перекрёстная клавиша — отдельный механизм серии.
3. Освещённость (оценка) — по норме СанПиН 1.2.3685-21 (табл. 5.52, на полу), не светотехнический расчёт; декоративная подсветка в оценку не входит.
4. За отметку 0,000 принят уровень чистого пола. Высоты Н — от чистого пола до оси изделия; привязки — от чистовой грани стены до оси механизма (у рамки на несколько постов — до оси рамки).
5. Розеточные и мокрые линии — через УЗО или дифавтомат с током утечки не более 30 мА (ПУЭ 7.1.79); в санузле выполнить ДСУП (ПУЭ 7.1.87–7.1.88).
6. Кабель — медный, исполнение нг(А)-LS (ГОСТ 31565-2012); скрытая прокладка только горизонтально и вертикально, фактические трассы зафиксировать исполнительной схемой до закрытия отделкой.
7. Расчёт нагрузок, токов КЗ, селективности и сечений — по проекту ЭОМ организации с допуском СРО; лист задаёт состав, расположение и группы.
8. Ведомости занимают 2 листов этого наименования: таблицы, не вошедшие в поле листа, продолжены на следующем листе.

Допущения и предложения на листе. Знак «**» предложено (согласовать). См. лист открытых вопросов (листы 6, 7).

Изм.	Кол.уч	Лист	№ док.	Подп.	Дата
Разраб.		Кырлан А.С.			13.11.26
Пров.					
ГИП					
Н. контр.					
Утв.					

ГД-2026-011-АИ

Квартира 56 м²

ЖК «Северный парк», Москва

Дизайн-проект интерьера

Стадия	Лист	Листов
РП	35	119

Ведомость электроточек и изделий

М б/м

Кырлан Александр Сергеевич

выпуск 13.11.2026 № eb78108814f · стр. 38 из 139

Ведомость электроточек и изделий (продолжение)

Электроточки, изделия, светильники, освещённость, клавиши выключателей · б/м

Расшифровка клавиш (продолжение)

Марка	Пом.	Н, мм	Клав.	Механизм	Группа: светильники
S7	1	900	1	светорегулятор	L12: Св31**, Св32**, Св33**, Св34**, Св35**, Св36**, Св37**, Св38**
S8**	1	900	1	светорегулятор	L14: Св42**, Св43**, Св44**
S9**	1	900	1	светорегулятор	L16: Св49**
S10	5	900	1	обычный	L4: Св12–Св14
			2	обычный	L5: Св15**
S11	5	900	1	проходной	L10: Св26–Св29
S12**	1	900	1	светорегулятор	L13: Св41
S13**	1	900	1	обычный	L15: Св45–Св48

Допущения и предложения на листе

Основа листа: размеры помещений и положение проёмов введены заказчиком в брифе, на объекте не замерены (К-1); высота потолка 2700 мм — по брифу заказчика, не замерена (К-2); толщины стен приняты по брифу: наружные 200 мм, внутренние 150 мм — не обмерены (К-1); тип дома монолитный, перекрытие 200 мм — по брифу заказчика, документов нет (К-3); планировка (стены, проёмы, объединение кухни и гостиной, расширение санузла) — по брифу без обмера и плана БТИ (К-7); разрешённая мощность 10 кВт принята, ТУ не переданы (К-8); вентканалы приняты, в брифе не заданы (К-9); подрайон климата не задан — принят не северный (жилые от 2,5 м) (К-10).

Знак «**» — предложение проектировщика, заказчиком не утверждено (согласовать с заказчиком): S12 — свой пост группе L13: сценарии «Вечер», «Ужин», «Кино», «Готовка» включают её отдельно от L12 — на одном светорегуляторе не набрать; S8, S9 — светорегулятор добавлен разработчиком проекта; S13 — свой пост группе L15: сценарии «Вечер», «Ужин», «Готовка» включают её отдельно от L14 — на одном светорегуляторе не набрать; Св31, Св32, Св33, Св34, Св35, Св36, Св37, Св38 — ряды — по зоне гостиной (по мебели); Св42, Св43, Св44, Св49 — диммируемость добавлена разработчиком проекта под светорегуляторы S8 и S9; Св15 — Сдвиг под раскладку плитки стены А на 52 мм вдоль стены — ось на шве или в центре плитки, привязка по таблице листа. См. лист открытых вопросов (лист 6, записи К-1–К-3, К-7–К-10).

Примечания

1. Продолжение ведомостей: лист 2 из 2 этого наименования; таблицы, прерванные на предыдущем листе, продолжены с заголовком «(продолжение)».
2. За отметку 0,000 принят уровень чистого пола. Высоты Н — от чистого пола до оси изделия; привязки — от чистовой грани стены до оси механизма (у рамки на несколько постов — до оси рамки).
3. Розеточные и мокрые линии — через УЗО или дифавтомат с током утечки не более 30 мА (ПУЭ 7.1.79); в санузле выполнить ДСУП (ПУЭ 7.1.87–7.1.88).
4. Кабель — медный, исполнение нг(А)-LS (ГОСТ 31565-2012); скрытая прокладка только горизонтально и вертикально, фактические трассы зафиксировать исполнительной схемой до закрытия отделкой.
5. Расчёт нагрузок, токов КЗ, селективности и сечений — по проекту ЭОМ организации с допуском СРО; лист задаёт состав, расположение и группы.

Изм.	Кол.уч	Лист	№ док.	Подп.	Дата
Разраб.		Кырлан А.С.			13.11.26
Пров.					
ГИП					
Н. контр.					
Утв.					

ГД-2026-011-АИ

Квартира 56 м²

ЖК «Северный парк», Москва

Дизайн-проект интерьера

Стадия	Лист	Листов
РП	36	119

Ведомость электроточек и изделий (продолжение)


М б/м

Кырлан Александр Сергеевич

выпуск 13.11.2026 № eb7810814f · стр. 39 из 139

Однолинейная схема щита

Щит квартирный ЩК · без масштаба

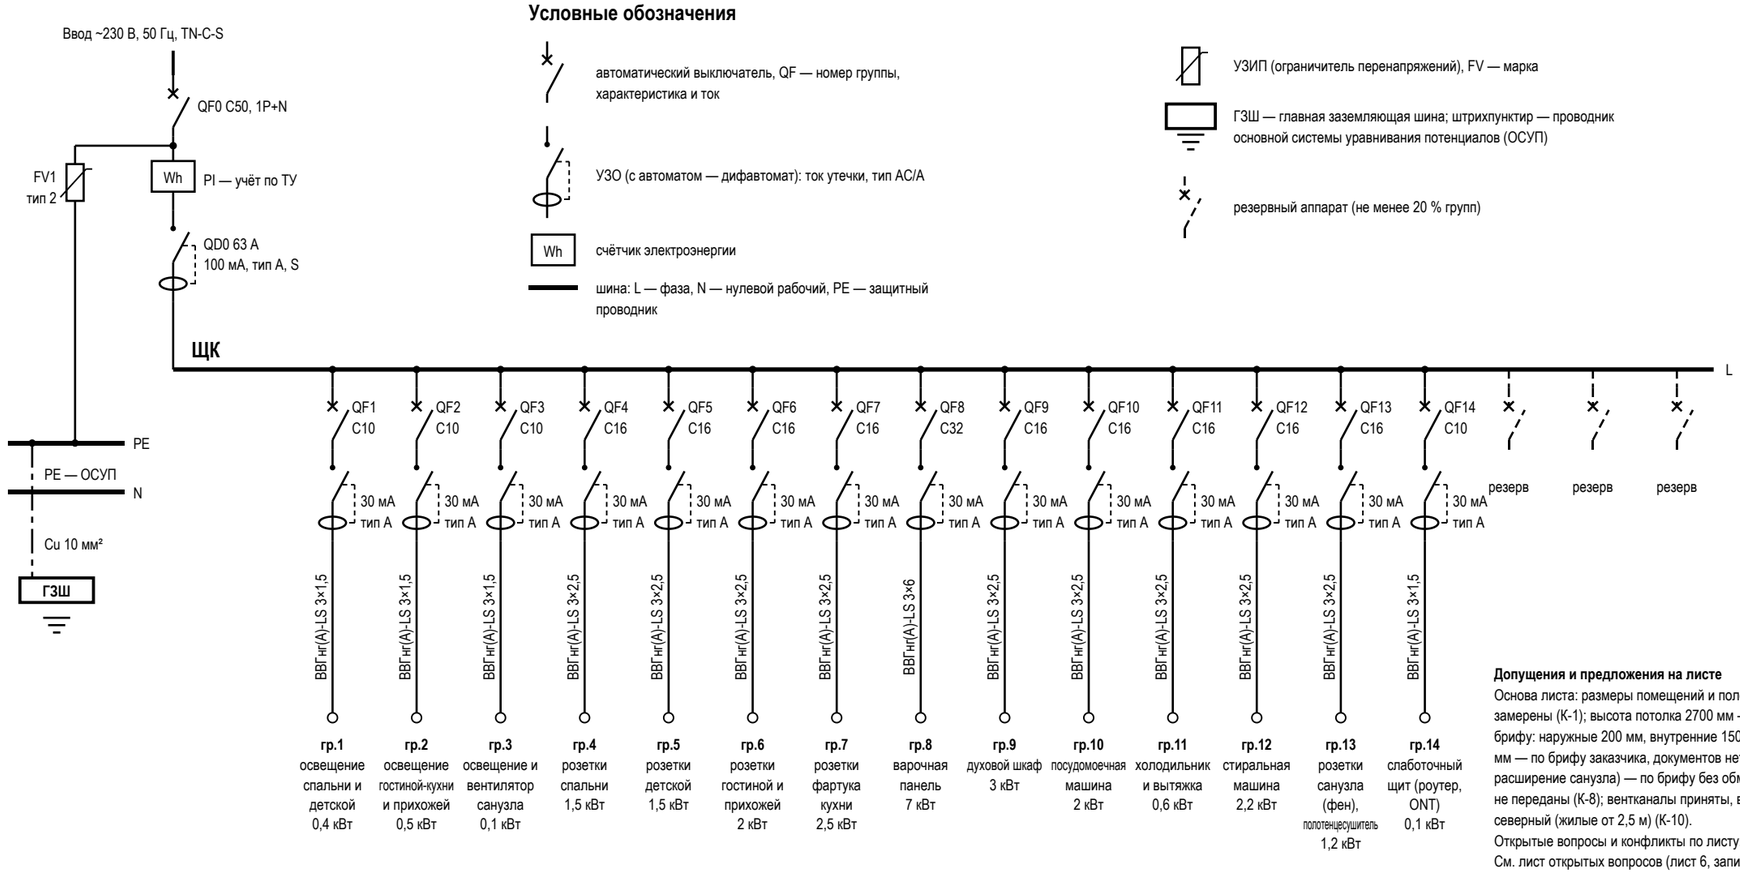

Условные обозначения

- автоматический выключатель, QF — номер группы, характеристика и ток
- УЗО (с автоматом — дифавтомат): ток утечки, тип AC/A
- Wh — счётчик электроэнергии
- шина: L — фаза, N — нулевой рабочий, PE — защитный проводник
- УЗИП (ограничитель перенапряжений), FV — марка
- ГЗШ — главная заземляющая шина; штрихпунктир — проводник основной системы уравнивания потенциалов (ОСУП)
- резервный аппарат (не менее 20 % групп)

Данные щитка

Показатель	Значение
Номер щитка	ЩК
Тип	ЩРВ-П-48, IP41
Уст. мощность, кВт	24,6
Разреш. мощность, кВт	10
Расчётная, кВт	9,6
Автоматы 1п: занят. / рез.	14 / 3
Модулей: всего / занято	48 / 34
Ток на вводе, А	50
Вводной аппарат	QF0 C50, 1P+N
УЗИП	FV1, тип 2, ЩК, после счётчика
ГЗШ, проводник ОСУП	Cu 10 мм²

Таблица групп щита ЩК и кабельный журнал

№	Назначение	Помещения	Автомат	УЗО / дифавтомат	Кабель	Длина, м	P, кВт	Точек
1	освещение спальни и детской	2, 3	C10	30 мА, тип A	ВВГнг(A)-LS 3×1,5	70,6	0,4	27
2	освещение гостиной-кухни и прихожей	1, 5	C10	30 мА, тип A	ВВГнг(A)-LS 3×1,5	71,9	0,5	32
3	освещение и вентилятор санузла	4, 5	C10	30 мА, тип A	ВВГнг(A)-LS 3×1,5	15,7	0,1	6
4	розетки спальни	2	C16	30 мА, тип A	ВВГнг(A)-LS 3×2,5	24,9	1,5	6
5	розетки детской	3	C16	30 мА, тип A	ВВГнг(A)-LS 3×2,5	20,5	1,5	4
6	розетки гостиной и прихожей	1, 5	C16	30 мА, тип A	ВВГнг(A)-LS 3×2,5	43,2	2	9
7	розетки фартука кухни	1	C16	30 мА, тип A	ВВГнг(A)-LS 3×2,5	29,6	2,5	6
8	варочная панель	1	C32	30 мА, тип A	ВВГнг(A)-LS 3×6	16,5	7	1
9	духовой шкаф	1	C16	30 мА, тип A	ВВГнг(A)-LS 3×2,5	16,5	3	1
10	посудомоечная машина	1	C16	30 мА, тип A	ВВГнг(A)-LS 3×2,5	14	2	1
11	холодильник и вытяжка	1	C16	30 мА, тип A	ВВГнг(A)-LS 3×2,5	16,3	0,6	2
12	стиральная машина	4	C16	30 мА, тип A	ВВГнг(A)-LS 3×2,5	7,5	2,2	1
13	розетки санузла (фен), полотенцесушитель	4	C16	30 мА, тип A	ВВГнг(A)-LS 3×2,5	13,6	1,2	2
14	слаботочный щит (роутер, ONT)	5	C10	30 мА, тип A	ВВГнг(A)-LS 3×1,5	5,4	0,1	1
	Итого по сечениям ВВГнг(A)-LS, м: 3×1,5 — 163,6; 3×2,5 — 186,1; 3×6 — 16,5					366,2		

Допущения и предложения на листе

Основа листа: размеры помещений и положение проёмов введены заказчиком в брифе, на объекте не замерены (К-1); высота потолка 2700 мм — по брифу заказчика, не замерена (К-2); толщины стен приняты по брифу: наружные 200 мм, внутренние 150 мм — не обмерены (К-1); тип дома монолитный, перекрытие 200 мм — по брифу заказчика, документов нет (К-3); планировка (стены, проёмы, объединение кухни и гостиной, расширение санузла) — по брифу без обмера и плана БТИ (К-7); разрешённая мощность 10 кВт принята, ТУ не переданы (К-8); вентканалы приняты, в брифе не заданы (К-9); подрайон климата не задан — принят не северный (жилые от 2,5 м) (К-10).

Открытые вопросы и конфликты по листу: К-8.

См. лист открытых вопросов (лист 6, записи К-1–К-3, К-7–К-10).

Примечания

1. Схема однолинейная: одна линия — фаза, N и PE группы; аппараты — в отключённом положении (ГОСТ 2.702, ГОСТ 2.755). Номера групп — как у точек на планах (гр.). За отметку 0,000 принят уровень чистого пола; высота щита — по плану розеток.
2. Розеточные и мокрые линии — через УЗО или дифавтомат с током утечки не более 30 мА (ПУЭ 7.1.79); в санузле выполнить ДСУП (ПУЭ 7.1.87–7.1.88).
3. УЗО тип A — для линий с электроникой, стиральной и посудомоечной машиной, LED-драйверами; тип AC — только для чисто активной нагрузки.
4. Кабель — медный, исполнение нг(A)-LS (ГОСТ 31565-2012); скрытая прокладка только горизонтально и вертикально, фактические трассы зафиксировать исполнительной схемой до закрытия отделкой.
5. Номинал автомата — не выше допустимого тока кабеля: 1,5 мм² — до 10 А, 2,5 мм² — до 16 А. Резерв щита — не менее 20 % модулей.
6. Расчёт нагрузок, токов КЗ, селективности и сечений — по проекту ЭОМ организации с допуском СРО; лист задаёт состав, расположение и группы.
7. УЗИП FV1 — после вводного автомата, проводник к шине PE — кратчайший, без петель. Шина PE щита соединяется с ГЗШ проводником ОСУП; к ГЗШ присоединяются трубы водопровода и отопления на вводе в квартиру (ПУЭ 7.1.87). Шины N и PE — раздельные, после разделения PEN не объединяются.
8. До подключения нагрузки — приёмо-сдаточные испытания с протоколом: сопротивление изоляции линий не менее 0,5 МОм, срабатывание УЗО по току и времени, непрерывность защитных проводников PE (ПУЭ, гл. 1.8).

Изм.	Кол.уч	Лист	№ док.	Подп.	Дата
Разраб.		Кырлан А.С.			13.11.26
Пров.					
ГИП					
Н. контр.					
Утв.					

ГД-2026-011-АИ

Квартира 56 м²

ЖК «Северный парк», Москва

Дизайн-проект интерьера

Стадия	Лист	Листов
РП	37	119

Однолинейная схема щита

М б/м


Кырлан Александр Сергеевич

План принципиальных трасс

Силовые трассы и объёмы электромонтажа, слаботочка в объёмах · размеры в мм

ПРЕДВАРИТЕЛЬНО · не для производства работ · открыто пунктов: 13 (реестр — л. 6, 7)

План принципиальных трасс (М 1:50)

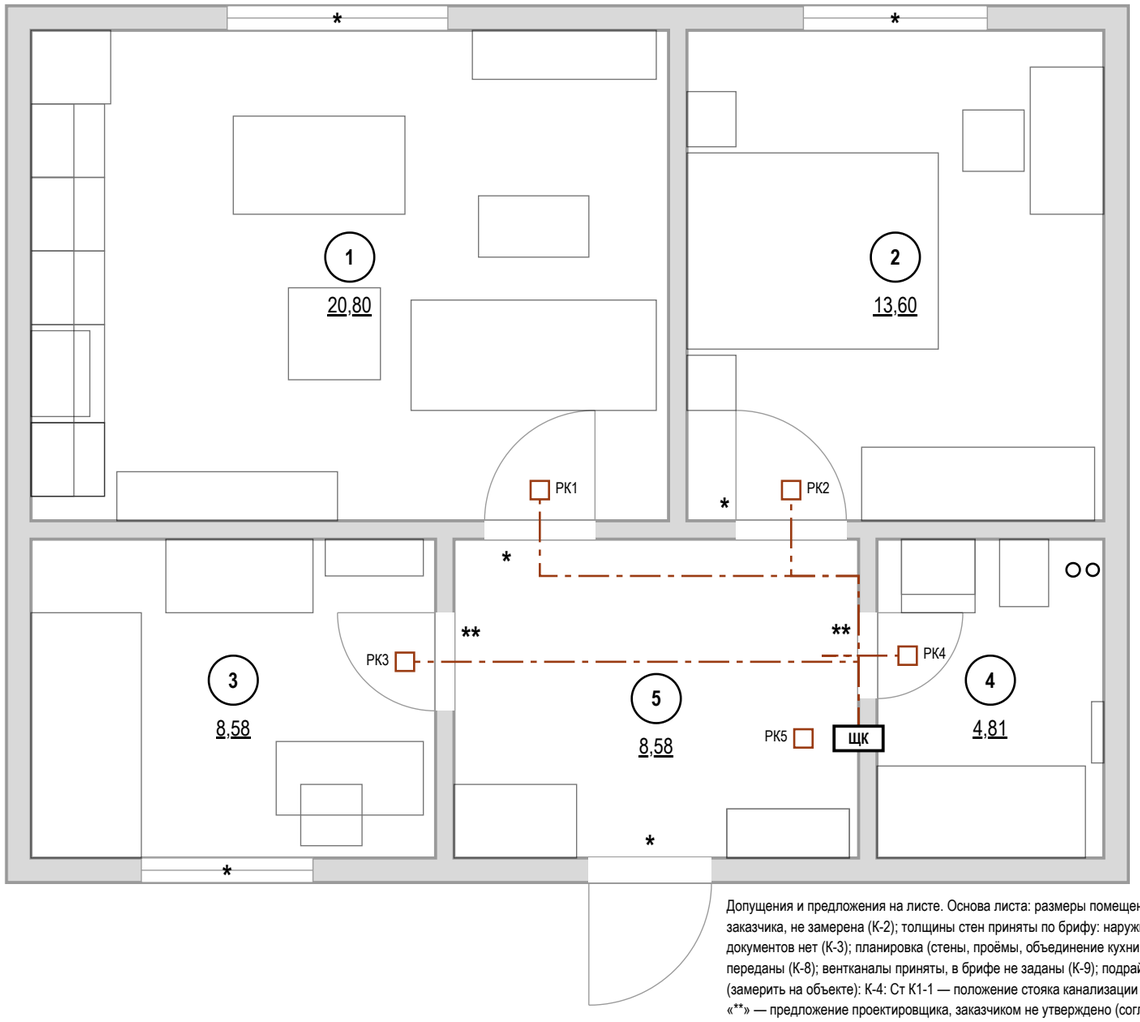

Допущения и предложения на листе. Основа листа: размеры помещений и положение проёмов введены заказчиком в брифе, на объекте не замерены (К-1); высота потолка 2700 мм — по брифу заказчика, не замерена (К-2); толщины стен приняты по брифу: наружные 200 мм, внутренние 150 мм — не обмерены (К-1); тип дома монолитный, перекрытие 200 мм — по брифу заказчика, документов нет (К-3); планировка (стены, проёмы, объединение кухни и гостиной, расширение санузла) — по брифу без обмера и плана БТИ (К-7); разрешённая мощность 10 кВт принята, ТУ не переданы (К-8); вентканалы приняты, в брифе не заданы (К-9); подрайон климата не задан — принят не северный (жилые от 2,5 м) (К-10). Знак «*» — принято, не замерено и не подтверждено (замерить на объекте): К-4: Ст К1-1 — положение стояка канализации — по брифу заказчика, не замерено; Ст В1-1 — положение стояка холодной воды — по брифу заказчика, не замерено. Знак «**» — предложение проектировщика, заказчиком не утверждено (согласовать с заказчиком): ЩС — щит слаботочный: место и состав. См. лист открытых вопросов (лист 6, записи К-1–К-5, К-7–К-10).

Кабель по группам ВВГнг(А)-LS, м

Гр.	мм²	Трасса	Данные
1	3×1,5	70,6	70,6
2	3×1,5	72,8	71,9
3	3×1,5	15,8	15,7
4	3×2,5	24,9	24,9
5	3×2,5	20,5	20,5
6	3×2,5	43,2	43,2
7	3×2,5	30,5	29,6

Гр.	мм²	Трасса	Данные
8	3×6	16,5	16,5
9	3×2,5	16,5	16,5
10	3×2,5	14	14
11	3×2,5	16,3	16,3
12	3×2,5	7,4	7,5
13	3×2,5	13,7	13,6
14	3×1,5	5,4	5,4
Σ		**368,1**	**366,2**

Экспликация помещений

№	Помещение	Площадь, м²
1	Гостиная-кухня	20,80
2	Спальня	13,60
3	Детская	8,58
4	Санузел	4,81
5	Прихожая	8,58
	Итого (общая площадь)	56,37

Объёмы прокладки

Работа, материал	Ед.	Кол.
Гофротруба Ø20 в потолочном пространстве	м	129,5
Кабель-канал плинтуса для силовых линий	м	95,3
Короб или накладной канал для вертикальных спусков и подъёмов	м	73,4
Коробка распределительная (РК) над дверью помещения	шт	5
Слаботочка: кабель домофона	м	6,7
Слаботочка: Кабель коаксиальный RG-6 (75 Ом) к розеткам ТВ	м	11,7
Слаботочка: U/UTP кат. 6 (LAN, Wi-Fi, камеры)	м	44,9
Слаботочка: гофротруба Ø20 отдельно от силовых	м	57

Штробы — только после заключения

Работа	Ед.	Кол.
Вертикальные штробы 20×20 мм от потолка до каждой настенной точки (в маршрут без штроб не входят)	м	91,05

Условные обозначения

- **ЩК** — щит квартирный
- РК — распределительная коробка над дверью помещения
- магистраль от щита к РК: потолочное пространство, гофра
- мебель и сантехприборы — подложка

Примечания

1. За отметку 0,000 принят уровень чистого пола. Высоты Н — от чистого пола до оси изделия; привязки — от чистовой грани стены до оси механизма (у рамки на несколько постов — до оси рамки).
2. Розеточные и мокрые линии — через УЗО или дифавтомат с током утечки не более 30 мА (ПУЭ 7.1.79); в санузле выполнить ДСУП (ПУЭ 7.1.87–7.1.88).
3. Кабель — медный, исполнение нг(А)-LS (ГОСТ 31565-2012); скрытая прокладка только горизонтально и вертикально, фактические трассы зафиксировать исполнительной схемой до закрытия отделкой.
4. Расчёт нагрузок, токов КЗ, селективности и сечений — по проекту ЭОМ организации с допуском СРО; лист задаёт состав, расположение и группы.
5. Длины — по плану: от щита вверх в потолочное пространство, по дверям и коридору без захода в мокрые помещения к распределительной коробке над дверью, далее к точкам; вертикали считаются вниз и обратно (у последней точки цепочки — в один конец); запас 10 %. Трассы принципиальные: фактическую зафиксировать исполнительной схемой до закрытия отделкой.
6. Несущие стены не определены: штробы в стенах не выполнять. Маршрут проложен без штроб: горизонтали — за потолком в гофре (129,5 м) и в кабель-канале плинтуса (95,3 м), вертикали — в коробе или накладном канале (129,2 м кабеля). Точек: за потолком — 43, спуск из потолка — 12, по плинтусу — 14, плинтус и подъём 30.
7. Вариант со штробами — работа после технического заключения: 91,05 м вертикальных штроб от потолка до каждой настенной точки; условие — только после технического заключения: стена не несущая (или вертикальная штроба в несущей согласована конструктором), глубина и ширина 20–25 мм, не в зонах 0–2 ванной. Без заключения и согласования конструктора в смету и в график эта работа не входит.
8. В данных проекта (журнал щита) длины кабеля внесены оценкой (366 м), по трассам из геометрии — 368 м (+1 %): к закупке и в смету принимать длины по трассам, а оценку в данных проекта заменить.
9. Слаботочные сети: кабели и точки считаются по лучам от ЩС** (лист слаботочных сетей): 63 м, портов патч-панели и коммутатора не менее 5; из точек 2 предложения листа слаботочки, не подтверждённые заказчиком. Изделия — в ведомости изделий.

1000 мм · печать 1:1

Изм.	Кол.уч	Лист	№ док.	Подп.	Дата
Разраб.		Кырлан А.С.			13.11.26
Пров.					
ГИП					
Н. контр.					
Утв.					

ГД-2026-011-АИ

Квартира 56 м²

ЖК «Северный парк», Москва

Дизайн-проект интерьера

Стадия	Лист	Листов
РП	38	119

План принципиальных трасс

М 1:50

Кырлан Александр Сергеевич

выпуск 13.11.2026 № eb7810814f · стр. 41 из 139

Таблица нагрузок щита

щит ЩК · 14 групп · Ррасч 9,6 кВт · без масштаба

Группы щита ЩК (1)

№	Назначение	Руст, кВт	Кс	Ррасч, кВт	Iрасч, А	Автомат	Кабель
1	освещение спальни и детской	0,4	0,6	0,24	1,1	C10	3×1,5
2	освещение гостиной-кухни и прихожей	0,5	0,6	0,3	1,4	C10	3×1,5
3	освещение и вентилятор санузла	0,1	0,6	0,06	0,3	C10	3×1,5
4	розетки спальни	1,5	0,4	0,6	2,7	C16	3×2,5
5	розетки детской	1,5	0,4	0,6	2,7	C16	3×2,5
6	розетки гостиной и прихожей	2	0,4	0,8	3,7	C16	3×2,5
7	розетки фартука кухни	2,5	0,4	1	4,6	C16	3×2,5

Группы щита ЩК (2)

№	Назначение	Руст, кВт	Кс	Ррасч, кВт	Iрасч, А	Автомат	Кабель
8	варочная панель	7	0,6	4,2	19,2	C32	3×6
9	духовой шкаф	3	0,6	1,8	8,2	C16	3×2,5
10	посудомоечная машина	2	0,7	1,4	6,4	C16	3×2,5
11	холодильник и вытяжка	0,6	0,4	0,24	1,1	C16	3×2,5
12	стиральная машина	2,2	0,7	1,54	7	C16	3×2,5
13	розетки санузла (фен), полотенцесушитель	1,2	0,7	0,84	3,8	C16	3×2,5
14	слаботочный щит (роутер, ONT)	0,1	0,4	0,04	0,2	C10	3×1,5

Итог по квартире

Показатель	Значение
Установленная мощность Σ Руст	24,6 кВт
Σ Руст × Кс по группам	13,66 кВт
Коэффициент одновременности	0,7
Расчётная мощность квартиры Ррасч	9,6 кВт
Расчётный ток Iрасч (230 В, cosφ 0,95)	44 А
Разрешённая мощность	10 кВт
Запас до разрешённой	4,4 % — меньше 10 %
Вводной аппарат	C50, 1P+N

Примечания

1. Руст — установленная мощность группы по данным щита (приборы — по паспорту, розетки общего назначения — оценка 0,1 кВт на гнездо). Кс — коэффициенты спроса: освещение 0,6; розетки 0,4; варочная и духовой 0,6; кондиционеры 0,8; тёплый пол 1,0; прочие 0,7; одновременность 0,7.
2. Коэффициенты — ориентир исполнителя, не табличные значения нормы; расчёт нагрузки подтверждает инженер ЭОМ (СП 256.1325800.2016). Под разрешённую мощность они не подгоняются.
3. Вывод: запас 4,4 % < 10 % (расчётная 9,6 кВт при разрешённой 10 кВт). Это вопрос заказчику (реестр К-N): запросить увеличение мощности у сетевой организации либо принять приоритетное отключение нагрузок (тёплый пол, кондиционеры, вторая машина) при работе плиты.
4. Розеточные и мокрые линии — через УЗО или дифавтомат с током утечки не более 30 мА (ПУЭ 7.1.79); в санузле выполнить ДСУП (ПУЭ 7.1.87–7.1.88).

Допущения и предложения на листе

Основа листа: размеры помещений и положение проёмов введены заказчиком в брифе, на объекте не замерены (К-1); высота потолка 2700 мм — по брифу заказчика, не замерена (К-2); толщины стен приняты по брифу: наружные 200 мм, внутренние 150 мм — не обмерены (К-1); тип дома монолитный, перекрытие 200 мм — по брифу заказчика, документов нет (К-3); планировка (стены, проёмы, объединение кухни и гостиной, расширение санузла) — по брифу без обмера и плана БТИ (К-7); разрешённая мощность 10 кВт принята, ТУ не переданы (К-8); вентканалы приняты, в брифе не заданы (К-9); подрайон климата не задан — принят не северный (жилые от 2,5 м) (К-10).
См. лист открытых вопросов (лист 6, записи К-1–К-3, К-7–К-10).


Изм.	Кол.уч	Лист	№ док.	Подп.	Дата				
Разраб.		Кырлан А.С.			13.11.26	ГД-2026-011-АИ			
Пров.						Квартира 56 м² ЖК «Северный парк», Москва			
ГИП						Дизайн-проект интерьера	Стадия	Лист	Листов
							РП	39	119
Н. контр.						Таблица нагрузок щита М б/м	Кырлан Александр Сергеевич		
Утв.									

выпуск 13.11.2026 № eb7810814f · стр. 42 из 139

План слаботочных сетей

Интернет, ТВ, домофон · размеры в мм · высоты от чистого пола

План слаботочных сетей (М 1:50)

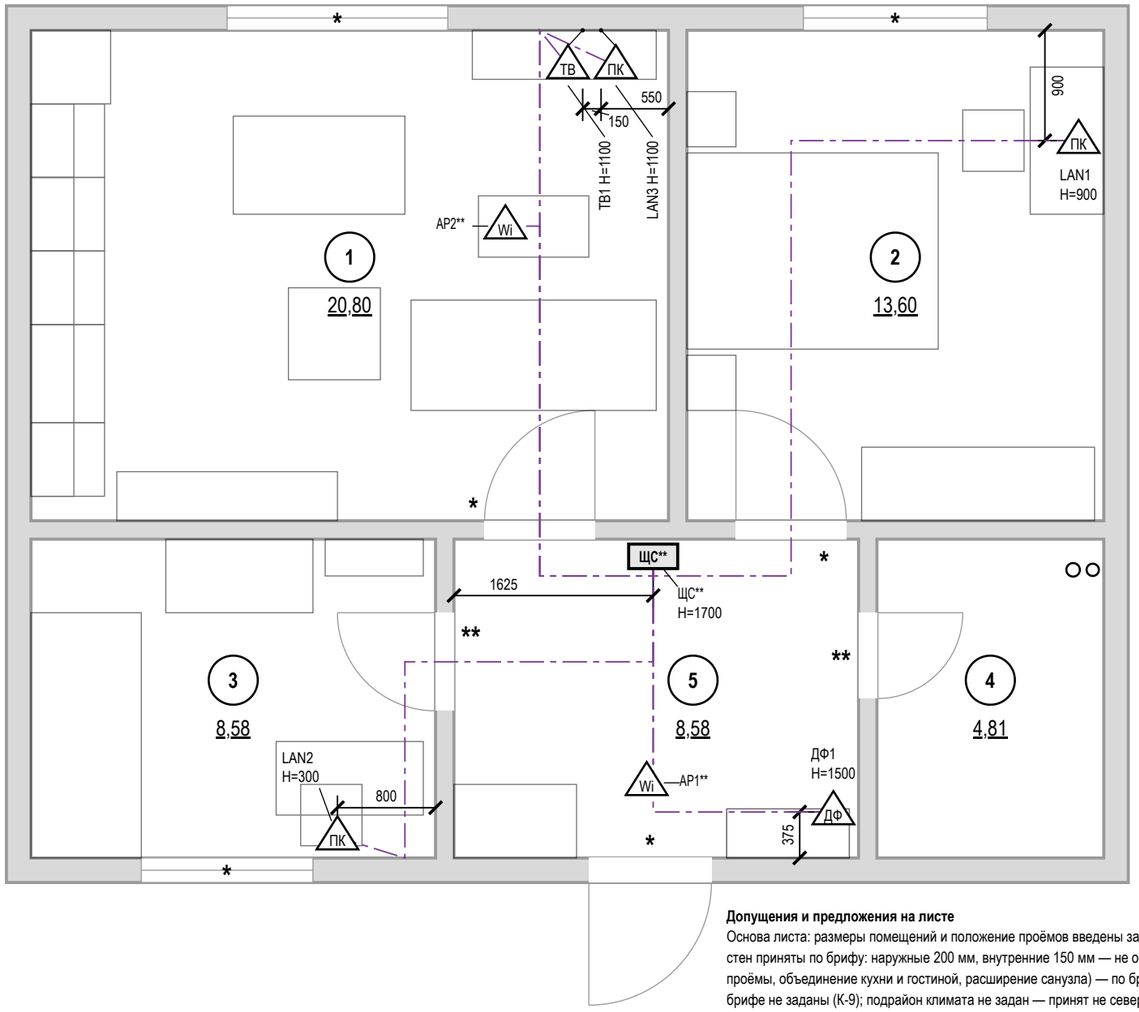

Допущения и предложения на листе

Основа листа: размеры помещений и положение проёмов введены заказчиком в брифе, на объекте не замерены (К-1); высота потолка 2700 мм — по брифу заказчика, не замерена (К-2); толщины стен приняты по брифу: наружные 200 мм, внутренние 150 мм — не обмерены (К-1); тип дома монолитный, перекрытие 200 мм — по брифу заказчика, документов нет (К-3); планировка (стены, проёмы, объединение кухни и гостиной, расширение санузла) — по брифу без обмера и плана БТИ (К-7); разрешённая мощность 10 кВт принята, ТУ не переданы (К-8); вентканалы приняты, в брифе не заданы (К-9); подрайон климата не задан — принят не северный (жилые от 2,5 м) (К-10).

Знак «*» — принято, не замерено и не подтверждено (замерить на объекте): К-1: окно пом. 1 (стена А) — окно: положение, ширина, высота и подоконник — по брифу заказчика, не замерены; ограждение 900 мм — предложение исполнителя; дверь пом. 1 (стена В) — Петли у правого откоса (х 4600): открытое полотно стоит у стены Б, вошедший идёт влево к кухне; при петлях слева полотно запирало вход в карман между собой, диваном Гс2 и стеной Б; окно пом. 2 (стена А), 3 (В) — окно: положение, ширина, высота и подоконник — по брифу заказчика, не замерены; дверь пом. 2 (стена В) — проём в существующей стене между пом. 2 и 5: положение и ширина — по брифу заказчика, не замерены; дверь пом. 5 (стена В) — входная дверь: положение и ширина проёма — по брифу заказчика, не замерены; К-4: Ст К1-1 — положение стояка канализации — по брифу заказчика, не замерено; Ст В1-1 — положение стояка холодной воды — по брифу заказчика, не замерено.

Знак «**» — предложение проектировщика, заказчиком не утверждено (согласовать с заказчиком): AP2, AP1 — точка доступа Wi-Fi: число и места; ЩС — щит слаботочный: место и состав; К-5: дверь пом. 3 (стена Б), 4 (Г) — дверь в новой перегородке: проём по брифу, короб скрытой двери и размер в свету — после выбора модели и утверждения перегородки (К-5).

См. лист открытых вопросов (лист 6, записи К-1–К-5, К-7–К-10).

ПРЕДВАРИТЕЛЬНО · не для производства работ · открыто пунктов: 13 (реестр — л. 6, 7)

Ведомость слаботочных точек

Марка	Пом.	Назначение	H, мм	Кабель
TB1	1	розетка ТВ	1100	RG-6
LAN3	1	розетка LAN (RJ45)	1100	U/UTP кат. 6
AP2**	1	точка доступа Wi-Fi		U/UTP кат. 6
LAN1	2	розетка LAN (RJ45)	900	U/UTP кат. 6
LAN2	3	розетка LAN (RJ45)	300	U/UTP кат. 6
ЩС**	5	щит слаботочный	1700	ввод пров.
ДФ1	5	домофон (трубка)	1500	по системе
AP1**	5	точка доступа Wi-Fi		U/UTP кат. 6

Условные обозначения

- ЩС — щит слаботочный: ввод провайдера, роутер, коммутатор
- ПК — розетка компьютерная RJ45
- ТВ — розетка телевизионная
- ДФ — трубка или монитор домофона
- Wi — точка доступа Wi-Fi (питание PoE)
- кабель от ЩС до точки, отдельным лучом
- мебель и сантехприборы — подложка
- стояк: К1 — канализация, В1 — ХВС, Т3 — ГВС
- 1 — номер помещения, площадь м²

Примечания

1. За отметку 0,000 принят уровень чистого пола. Высоты Н — от чистого пола до оси изделия; привязки — от чистовой грани стены до оси механизма (у рамки на несколько постов — до оси рамки).
2. Высота установки, не указанная на плане: розетки LAN и ТВ — 300 мм от чистого пола.
3. Слаботочные кабели — отдельно от силовых: в своей трубе или лотке, при параллельной прокладке не ближе 100 мм к силовым, пересечения под прямым углом; каждую точку — отдельным кабелем от ЩС** без скруток.
4. Трассы на листе — принципиальные; фактические зафиксировать исполнительной схемой до закрытия отделкой. Силовые линии, УЗО 30 мА, ДСУП, кабель нг(А)-LS — по листам розеток и щита.
5. Проект силовой части и расчёт токов КЗ — по проекту ЭОМ; слаботочная часть согласуется с провайдером и управляющей компанией (домофон, коллективное ТВ).

1000 мм · печать 1:1

Изм.	Кол.уч	Лист	№ док.	Подп.	Дата
Разраб.		Кырлан А.С.			13.11.26
Пров.					
ГИП					
Н. контр.					
Утв.					

ГД-2026-011-АИ

Квартира 56 м²

ЖК «Северный парк», Москва

Дизайн-проект интерьера

Стадия	Лист	Листов
РП	40	119

План слаботочных сетей

М 1:50

Кырлан Александр Сергеевич

выпуск 13.11.2026 № eb7810814f · стр. 43 из 139

04

Отопление и вентиляция


Кырлан Александр Сергеевич

выпуск 13.11.2026 · eb7810814f · стр. 44 из 139

План вентиляции

Вытяжка, приток, переток · кондиционирование не предусмотрено · размеры в мм · высоты от чистого пола

План вентиляции (М 1:50)

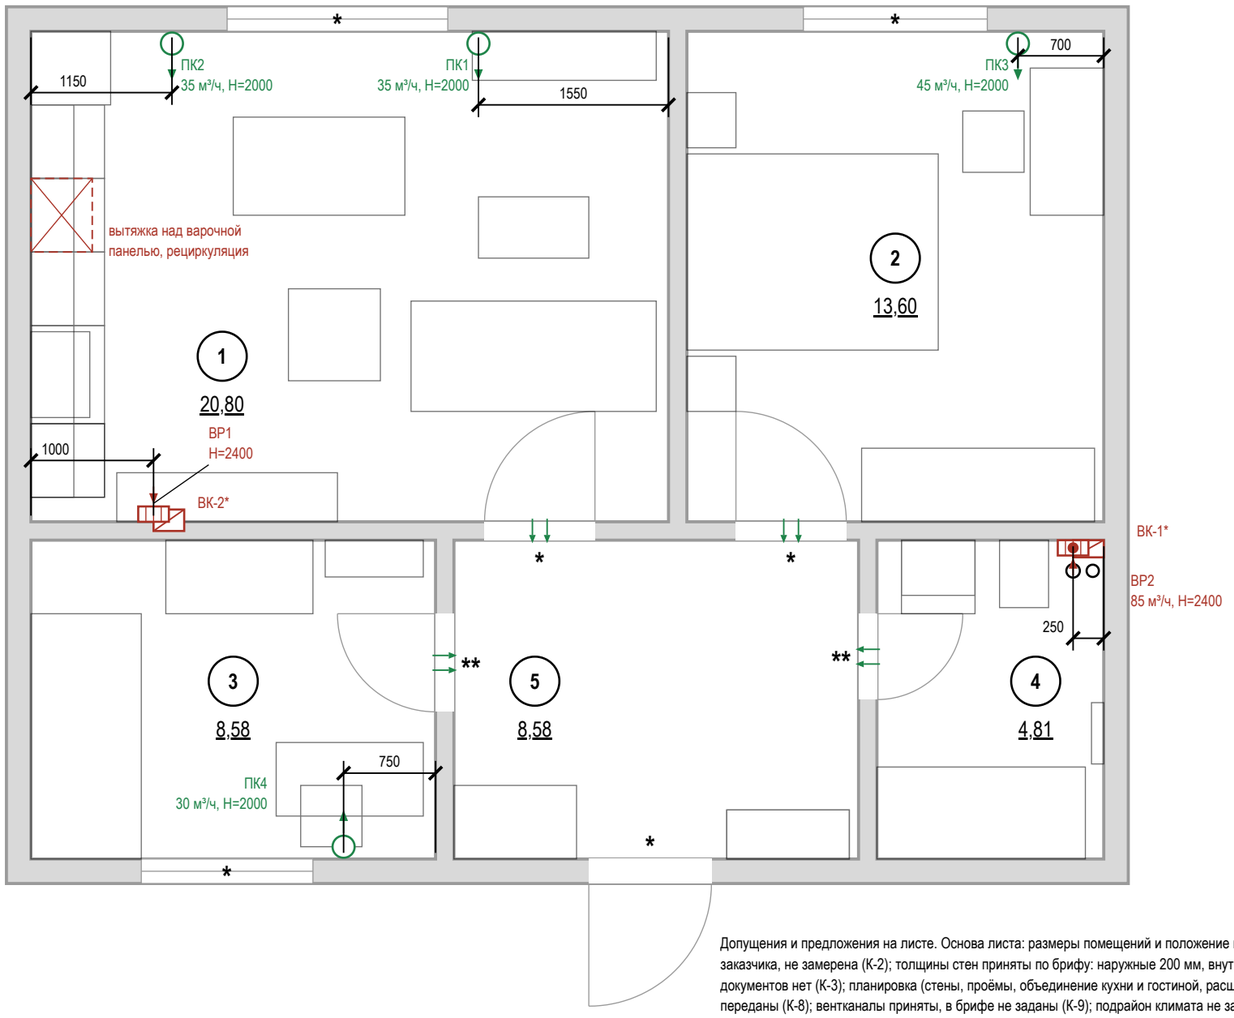

Условные обозначения

- стояк: К1 — канализация, В1 — ХВС, Т3 — ГВС
- номер помещения, площадь м²
- вытяжная решётка в вентканал: марка, расход м³/ч, H центра от чистого пола
- вытяжная решётка с бытовым вентилятором и обратным клапаном: марка, расход, H
- приточный клапан (КИВ) в наружной стене: марка, расход, H центра
- переток: зазор под полотном или переточная решётка
- кухонная вытяжка над варочной панелью
- вентканал ВК-N; «*» — принят до обмера
- * — «*» — принято, не замерено и не подтверждено
- ** — «**» — предложение проектировщика, заказчиком не утверждено

Воздухообмен, м³/ч

№	Помещение	Выт. норма	Выт. проект	Прит. норма	Прит. проект	Устрой-ства
1	Гостиная-кухня	60	60	63	70	ВР1, ПК1, ПК2
2	Спальня			41	45	ПК3
3	Детская			26	30	ПК4
4	Санузел	50	85			ВР2
	Итого	**110**	**145**	**130**	**145**	

Воздухообмен квартиры — по большей из сумм притока и вытяжки: норма 130 м³/ч, проект 145 м³/ч.
Вытяжка не меньше притока — баланс сведён.

Привязки — до обмера
Вентканалы ВК-N* приняты проектировщиком, решётки и воздуховоды — от них. До черновых работ — обмер каналов и тяги, лист перевыпустить по факту.

Допущения и предложения на листе. Основа листа: размеры помещений и положение проёмов введены заказчиком в брифе, на объекте не замерены (К-1); высота потолка 2700 мм — по брифу заказчика, не замерена (К-2); толщины стен приняты по брифу: наружные 200 мм, внутренние 150 мм — не обмерены (К-1); тип дома монолитный, перекрытие 200 мм — по брифу заказчика, документов нет (К-3); планировка (стены, проёмы, объединение кухни и гостиной, расширение санузла) — по брифу без обмера и плана БТИ (К-7); разрешённая мощность 10 кВт принята, ТУ не переданы (К-8); вентканалы приняты, в брифе не заданы (К-9); подрайон климата не задан — принят не северный (жилые от 2,5 м) (К-10). Знак «*» — принято, не замерено и не подтверждено (замерить на объекте): К-4: Ст К1-1 — положение стояка канализации — по брифу заказчика, не замерено; Ст В1-1 — положение стояка холодной воды — по брифу заказчика, не замерено. Знак «**» — предложение проектировщика, заказчиком не утверждено (согласовать с заказчиком). См. лист открытых вопросов (лист 6, записи К-1–К-5, К-7–К-10); по листу — К-9.

Примечания

1. Расчёт систем ОВ и подбор оборудования — проектная организация с допуском СРО; лист даёт места, трассы и привязки.
2. Нормы вытяжки — СП 54.13330.2022 (Изм. 1, 2), табл. 7.1: кухня с электроплитой 60 м³/ч, с газовой 100; ванная и совмещённый санузел 50; уборная 25; гардеробная 0,2 ч⁻¹. Приток в жилые — 3 м³/ч на 1 м² (менее 20 м² общей площади на человека), иначе 30 м³/ч на человека.
3. Вентканалы и шахты не сужать, не переносить и не закрывать; вентилятор и кухонная вытяжка — через обратный клапан, без перекрытия естественной тяги.
4. Проектные расходы — не ниже нормы, вытяжка сведена с притоком вентиляторами мокрых помещений. Клапаны — в простенке у окна, центр 2000 мм, не над кроватью, не ближе 300 мм к стоякам отопления; типоразмер — на расход.
5. Гостиная-кухня (пом. 1): вытяжка над варочной панелью рециркуляционная — без воздуховода, короба и входа в канал, в воздухообмен не включена; естественная тяга через решётку канала сохраняется. Отвод в канал — только вариантом по реестру (после обмера канала).
6. Переток — зазор под полотнами межкомнатных дверей или переточная решётка.
7. Кондиционирование заданием не предусмотрено; при установке трассы фреона и дренажа (не менее 40 мм/м, в К1 через сифон) и питание заложить до черновых работ.
8. Привязки оборудования — по паспортам приобретённых моделей, до черновых работ.
9. Знак «*» у проёма — допущение: положение проёма не замерено (окно пом. 1, стена А; дверь пом. 1, стена В; окно пом. 2, стена А; дверь пом. 2, стена В; окно пом. 3, стена В; дверь пом. 5, стена В); размер напечатан как принятый. Реестр: листы 6–7, вопросы К-1, К-11.
10. Клапаны ПК1, ПК2, ПК3, ПК4 выведены в простенок у окна, положение которого — допущение (знак «*»): после обмера окна привязку сверить.

1000 мм · печать 1:1

Изм.	Кол.уч	Лист	№ док.	Подп.	Дата
Разраб.		Кырлан А.С.			13.11.26
Пров.					
ГИП					
Н. контр.					
Утв.					

ГД-2026-011-АИ

Квартира 56 м²

ЖК «Северный парк», Москва

Дизайн-проект интерьера

Стадия	Лист	Листов
РП	41	119

План вентиляции

М 1:50

Кырлан Александр Сергеевич


ПРЕДВАРИТЕЛЬНО · не для производства работ · открыто пунктов: 13 (реестр — л. 6, 7)

выпуск 13.11.2026 № eb7810814f · стр. 45 из 139

План отопления

Радиаторы, стояки, подводки · размеры в мм · высоты от чистого пола

План отопления (М 1:50)

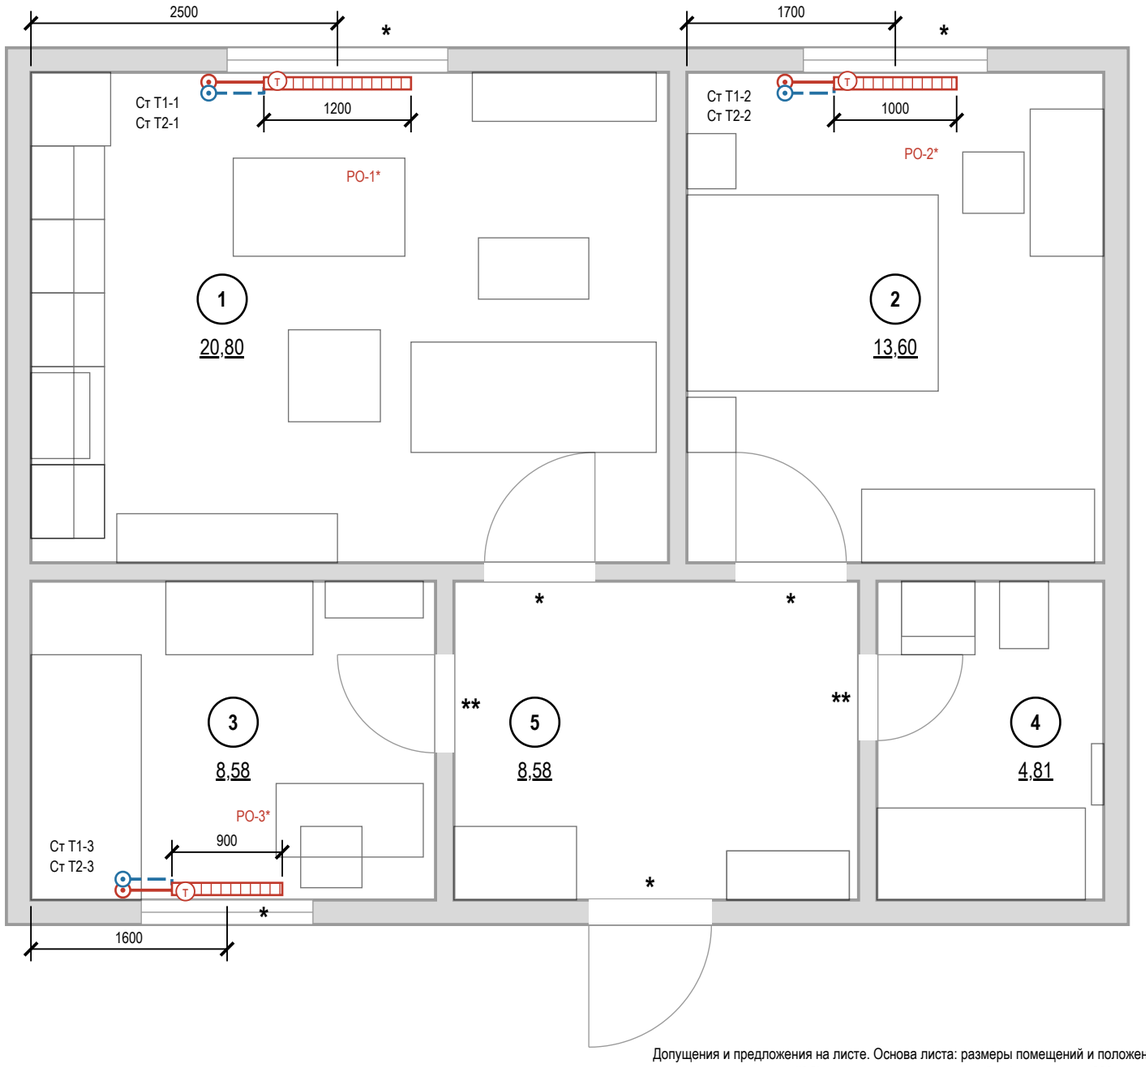

ПРЕДВАРИТЕЛЬНО · не для производства работ · открыто пунктов: 13 (реестр — л. 6, 7)

Условные обозначения

- (1) — номер помещения, площадь м²
- радиатор отопления (марка РО-N, длина по плану)
- (Т) — клапан с термоголовкой на подаче
- стояк отопления, подающий (Ст Т1-N)
- стояк отопления, обратный (Ст Т2-N)
- Т1 — отопление, подающий трубопровод
- Т2 — отопление, обратный трубопровод
- * — «*» — принято, не замерено и не подтверждено
- ** — «**» — предложение проектировщика, заказчиком не утверждено

Ведомость радиаторов

Марка	Помещение	Тип	Д×В×Г, мм	Низ / стена	Q, Вт
РО-1	1. Гостиная-кухня	панельный*	1200×600×100	120 / 40	расч.
РО-2	2. Спальня	панельный*	1000×600×100	120 / 40	расч.
РО-3	3. Детская	панельный*	900×600×100	120 / 40	расч.

* тип и мощность — по теплотехническому расчёту
Низ — от чистого пола, стена — зазор до задней панели, мм.

Привязки — до обмера
Стояки отопления в исходных данных не заданы: показаны у откосов окон, подводки — принципиально. До черновых работ — обмер стояков и паспорта приборов; лист перевыпустить по факту.

Допущения и предложения на листе. Основа листа: размеры помещений и положение проёмов введены заказчиком в брифе, на объекте не замерены (К-1); высота потолка 2700 мм — по брифу заказчика, не замерена (К-2); толщины стен приняты по брифу: наружные 200 мм, внутренние 150 мм — не обмерены (К-1); тип дома монолитный, перекрытие 200 мм — по брифу заказчика, документов нет (К-3); планировка (стены, проёмы, объединение кухни и гостиной, расширение санузла) — по брифу без обмера и плана БТИ (К-7); разрешённая мощность 10 кВт принята, ТУ не переданы (К-8); вентканалы приняты, в брифе не заданы (К-9); подрайон климата не задан — принят не северный (жилые от 2,5 м) (К-10). Знак «*» — принято, не замерено и не подтверждено (замерить на объекте). Знак «**» — предложение проектировщика, заказчиком не утверждено (согласовать с заказчиком). См. лист открытых вопросов (лист 6, записи К-1–К-3, К-5, К-7–К-10).

Примечания

1. Расчёт системы отопления, теплопотерь и подбор приборов — проектная организация с допуском СРО; лист даёт места и привязки.
2. Тип, длина и мощность радиаторов — по теплотехническому расчёту; лист задаёт места, зазоры и подключение.
3. Радиаторы — под каждым окном жилых комнат и кухни, центр по оси проёма, длина 0,7 ширины окна (кратно 100); окончательно — по расчёту.
4. Зазоры радиатора: низ не менее 100 мм от чистого пола, верх не менее 100 мм до подоконника, 30–50 мм от стены до задней панели; центр по оси окна с допуском ±20 мм. Верх до подоконника — 180 мм (РО-1 — 130).
5. Радиаторы не закрывать глухими коробами и мебелью; перенос и замена приборов в многоквартирном доме — переустройство, согласование с управляющей организацией (ЖК РФ ст. 25–26); вынос на лоджию запрещён.
6. Трубы отопления через межквартирные стены не прокладывать (СП 51.13330.2011, п. 9.19); через перекрытия и перегородки — в гильзах.
7. Привязки приборов и подводок — по паспортам приобретённых радиаторов и клапанов, до черновых работ.
8. До закрытия отделкой трубопроводы отопления испытать гидростатическим давлением с оформлением акта (СП 73.13330.2016, 7.2–7.3).
9. Знак «*» у проёма — допущение: положение проёма не замерено (окно пом. 1, стена А; дверь пом. 1, стена В; окно пом. 2, стена А; дверь пом. 2, стена В; окно пом. 3, стена В; дверь пом. 5, стена В); размер напечатан как принятый. Реестр: листы 6–7, вопросы К-1, К-11.
10. Радиаторы РО-1, РО-2, РО-3 стоят по оси окна, положение которого — допущение (знак «*»): после обмера окна привязки приборов и подводок сверить.

1000 мм · печать 1:1

Изм.	Кол.уч	Лист	№ док.	Подп.	Дата
Разраб.		Кырлан А.С.			13.11.26
Пров.					
ГИП					
Н. контр.					
Утв.					

ГД-2026-011-АИ

Квартира 56 м²

ЖК «Северный парк», Москва

Дизайн-проект интерьера

Стадия	Лист	Листов
РП	42	119

План отопления

М 1:50

Кырлан Александр Сергеевич

выпуск 13.11.2026 № eb7810814f · стр. 46 из 139

05

Водоснабжение и канализация

Кырлан Александр Сергеевич


выпуск 13.11.2026 · eb7810814f · стр. 47 из 139

План выводов сантехники


Выводы В1, Т3, К1 · привязки от чистовых стен · высоты от чистого пола, мм

ПРЕДВАРИТЕЛЬНО · не для производства работ · открыто пунктов: 13 (реестр — л. 6, 7)

Фрагмент 1. Гостиная-кухня, пом. 1 (М 1:20)

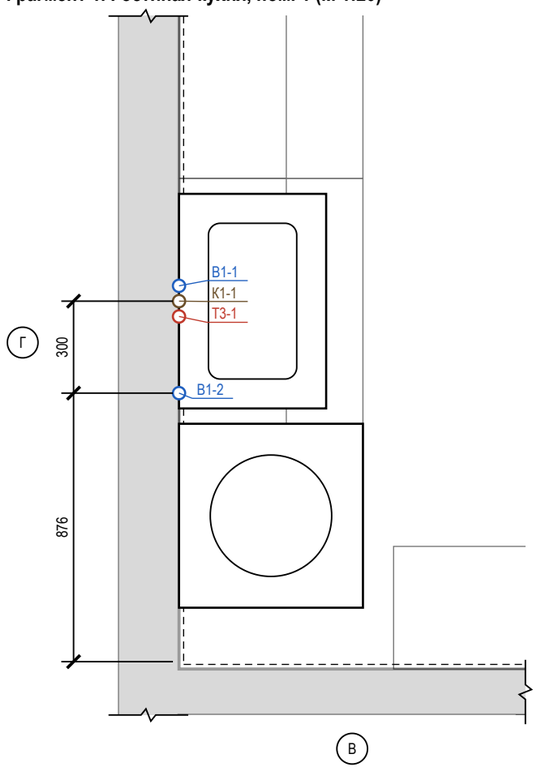

Фрагмент 2. Санузел, пом. 4 (М 1:20)

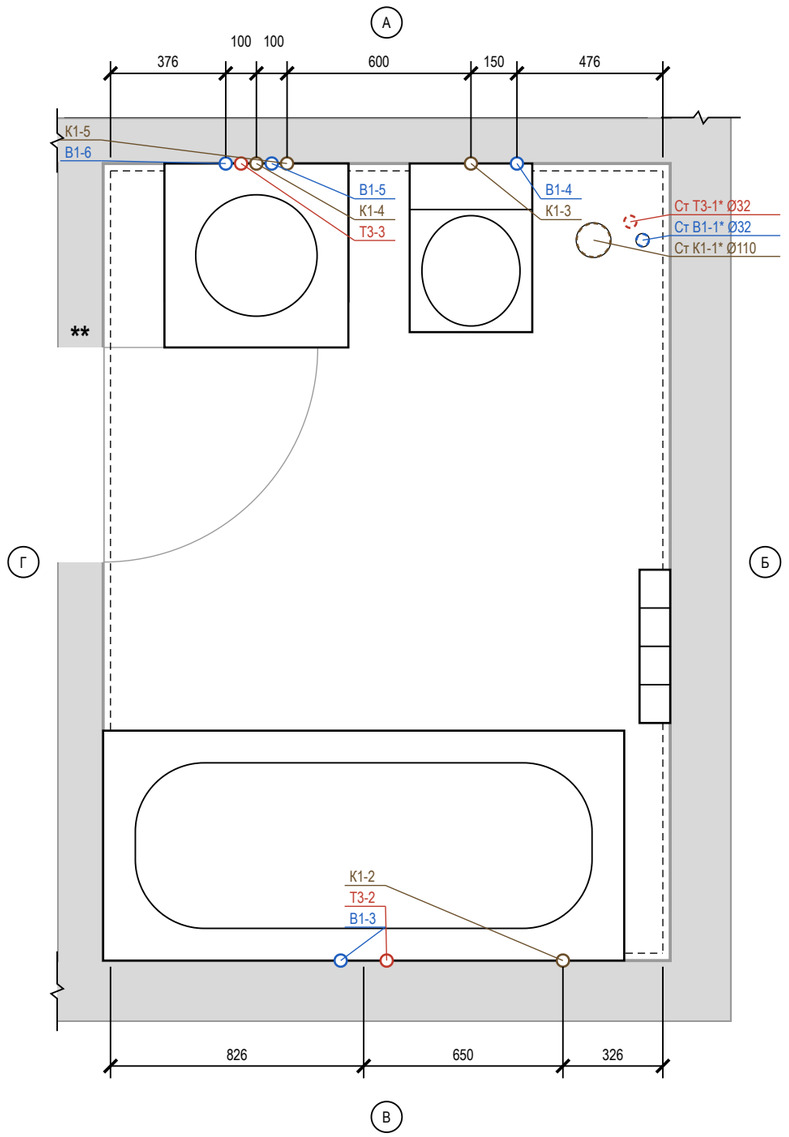

Ведомость привязок выводов

Код	Прибор	Ø	Н, мм	Привязка от чист. стен, мм	Прим.
В1-1	П1 мойка кухонная	½"	600*	ст. Г: 1226 от В	межос. 100
Т3-1	—"	½"	600*	ст. Г: 1126 от В	межос. 100
К1-1	—"	Ø50	400*	ст. Г: 1176 от В	
В1-2	П2 посудомоечная машина	½"	550*	ст. Г: 876 от В	кран ПММ в шкафу мойки
В1-3	Сн1 ванна	½"	800*	ст. В: 751 от Г	межос. 150
Т3-2	—"	½"	800*	ст. В: 901 от Г	межос. 150
К1-2	—"	Ø50	50*	ст. В: 326 от Б	
В1-4	Сн2 унитаз подвесной	½"	250*	ст. А: 476 от Б	в раме инсталляции
К1-3	—"	Ø110	220*	ст. А: 626 от Б	
В1-5	Сн3 умывальник	½"	950*	ст. А: 526 от Г	межос. 100
Т3-3	—"	½"	950*	ст. А: 426 от Г	межос. 100
К1-4	—"	Ø50	900*	ст. А: 476 от Г	плоский сифон, над машиной
В1-6	Сн4 стиральная машина	½"	600*	ст. А: 376 от Г	кран машины
К1-5	—"	Ø50	600*	ст. А: 576 от Г	

* — высота по практике монтажа; сверить по паспорту прибора

Условные обозначения

- вывод В1 (код — в ведомости привязок)
- вывод Т3 (код — в ведомости привязок)
- вывод К1 (код — в ведомости привязок)
- сантехприбор по расстановке (габарит модели)
- чистовая поверхность стены (от неё привязки)
- стояк «Ст К1-N / Ст В1-N» (ГОСТ 21.601), Ø мм
- * стояк Т3 не на обмере — принят в шахте рядом со Ст В1, сверить
- * у стояка — положение принято, не замерено, сверить
- линия обрыва (граница фрагмента)
- А обозначение стены А–Г (как на развёртках)

Допущения и предложения на листе

Основа листа: размеры помещений и положение проёмов введены заказчиком в брифе, на объекте не замерены (К-1); высота потолка 2700 мм — по брифу заказчика, не замерена (К-2); толщины стен приняты по брифу: наружные 200 мм, внутренние 150 мм — не обмерены (К-1); тип дома монолитный, перекрытие 200 мм — по брифу заказчика, документов нет (К-3); планировка (стены, проёмы, объединение кухни и гостиной, расширение санузла) — по брифу без обмера и плана БТИ (К-7); разрешённая мощность 10 кВт принята, ТУ не переданы (К-8); вентканалы приняты, в брифе не заданы (К-9); подрайон климата не задан — принят не северный (жилые от 2,5 м) (К-10).

Знак «*» — принято, не замерено и не подтверждено (замерить на объекте): К-4: Ст К1-1 — положение стояка канализации — по брифу заказчика, не замерено; Ст В1-1 — положение стояка холодной воды — по брифу заказчика, не замерено.

Знак «**» — предложение проектировщика, заказчиком не утверждено (согласовать с заказчиком): К-5: дверь пом. 4 (стена Г) — дверь в новой перегородке: проём по брифу, короб скрытой двери и размер в свету — после выбора модели и утверждения перегородки (К-5).

Открытые вопросы и конфликты по листу: К-4, К-9, К-11.

См. лист открытых вопросов (лист 6, записи К-1–К-5, К-7–К-10; лист 7, запись К-11).

Примечания

1. Привязки выводов даны от чистовых поверхностей стен (облицовка на сторону: гостиная-кухня — 24 мм (фартук: штукатурка 10 + клей 5 + плитка 9); санузел — 24 мм (штукатурка 10 + клей 5 + плитка 9)); эти же грани — на развёртках и в раскладке плитки. Высоты — от чистого пола помещения.
2. Высоты и межосевые, отмеченные «*», приняты по практике монтажа; до черновой разводки сверить по паспорту выбранного прибора (смеситель, инсталляция, сифон).
3. Горячая вода (Т3) — слева от холодной (В1), если смотреть на прибор. Допуск установки выводов: ±5 мм в группе, ±20 мм у отдельно стоящих.
4. Расчёт систем водоснабжения и канализации и подбор оборудования выполняет проектная организация; лист задаёт места и высоты выводов.
5. Посудомоечная машина П2: кран — отдельным выводом в шкафу мойки, слив — в отвод сифона мойки П1 (своего выпуска нет), шланг с петлёй выше сифона.
6. Раковина над стиральной машиной Сн3: плоский сифон, водорозетки и выпуск — над корпусом машины (высоты в таблице), не за ней.
7. Ст К1-1*, Ст В1-1*, Ст Т3-1 на обмере не показаны: приняты рядом с Ст В1-1* (в МКД стоят группой) (К-4); положение сверить на объекте до разметки.
8. Стояки в коробах/шахтах не замоноличивать; стояк К1 в коробе — звукоизоляция стояка в коробе без жёсткого контакта с трубой; к арматуре и ревизиям — люк не меньше 300×400.
9. Знак «*» у стояка — положение принято, не замерено (все стояки); сверить на объекте до разметки. Реестр: листы 6–7, вопрос К-4.

1000 мм · печать 1:1

Изм.	Кол.уч	Лист	№ док.	Подп.	Дата
Разраб.		Кырлан А.С.			13.11.26
Пров.					
ГИП					
Н. контр.					
Утв.					

ГД-2026-011-АИ

Квартира 56 м²

ЖК «Северный парк», Москва

Дизайн-проект интерьера

Стадия	Лист	Листов
РП	43	119

План выводов сантехники

М 1:20

Кырлан Александр Сергеевич


выпуск 13.11.2026 № eb7810814f · стр. 48 из 139

Схема разводки водопровода и канализации


Схемы систем В1, Т3, К1 · трассы принципиальные · уклоны в мм на 1 м · план М 1:200, фрагменты М 1:25

ПРЕДВАРИТЕЛЬНО · не для производства работ · открыто пунктов: 13 (реестр — л. 6, 7)


План квартиры (М 1:200)

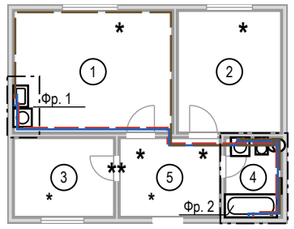

Фр. 1. Гостиная-кухня (М 1:25)

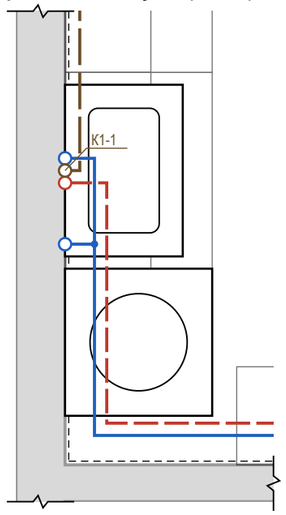

Фр. 2. Санузел (М 1:25)

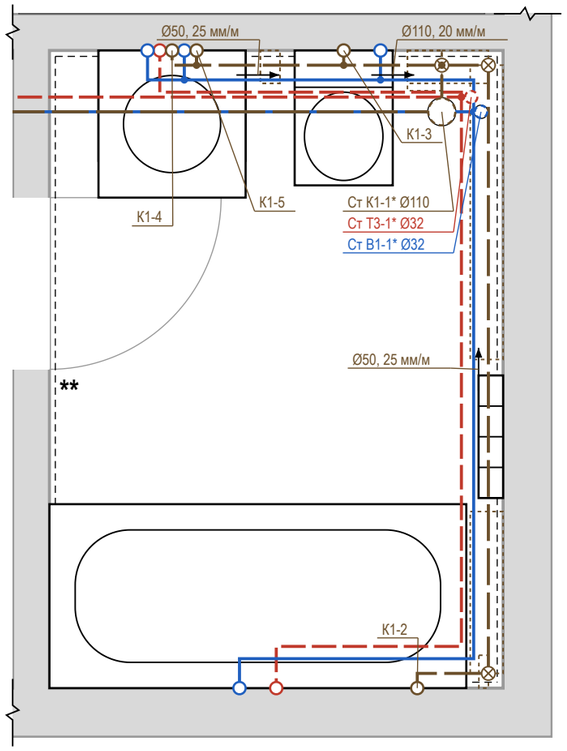

Условные обозначения

- В1 — водопровод хозяйственно-питьевой (ХВС), PP-R Ø20
- Т3 — горячее водоснабжение, подача (ГВС), PP-R Ø20
- К1 — канализация бытовая
- направление уклона К1 / пола: Ø, мм на 1 м
- ⊗ ревизия (прочистка) К1 — доступ сохранить
- ● тройник (ответвление к прибору)
- короб К1 над чистым полом (ГКЛВ под плитку)
- ○ вывод В1 (код — в ведомости привязок)
- ○ вывод Т3 (код — в ведомости привязок)
- ○ вывод К1 (код — в ведомости привязок)
- сантехприбор по расстановке (габарит модели)
- ○ стояк «Ст К1-N / Ст В1-N» (ГОСТ 21.601), Ø мм
- * стояк Т3 не на обмере — принят в шахте рядом со Ст В1, сверить
- * у стояка — положение принято, не замерено, сверить
- линия обрыва (граница фрагмента)
- граница фрагмента на плане (Фр. N)

Профиль выпусков К1 (до врезки в стояк)

Выпуск	Прибор	Ø	L, м	i, мм/м	Δh, мм	Прокладка, мм
К1-3	Сн2 унитаз подвесной	Ø110	0,65	20	13	короб 160×140
К1-1	П1 мойка кухонная	Ø50	15,58	25	390	через пом. 5: короба нет; К-11
К1-2	Сн1 ванна	Ø50	3,21	25	80	короб 160×110
К1-4	Сн3 умывальник	Ø50	1,35	25	34	короб 120×110
К1-5	Сн4 стиральная машина	Ø50	1,25	25	31	короб 120×110

Короб h×b: h — от чистого пола, b — от чистовой стены. Стяжка 35 мм — лист полов.

Узел ввода В1, Т3 (схема, без масштаба)



состав узла — по согласованию

⊗ Ст К1-1*: ревизия на стояке — люк в коробе

Примечания

1. Трассы принципиальные, построены от стояков вдоль стен помещений; фактическое положение фиксируется исполнительной схемой с привязками (фото с рулеткой) до закрытия.
2. Уклон К1 не менее 1/d и не более 150 мм/м (СП 30.13330.2020, п. 19.1), приняты практические уклоны; поворот — двумя отводами 45°, ревизия после поворота, доступ сохранить. Стояк К1 в коробе — звукоизоляция стояка в коробе, без жёсткого контакта короба с трубой.
3. Решение по К1: стяжка 35 мм не укрывает трубы (нужно Ø + Δh + 45 мм) — выпуски идут над чистым полом вдоль стен; К1-3, К1-2, К1-4, К1-5 — в коробе ГКЛВ под плитку (размеры в профиле). Короба — на развёртках; отметку низа врезки в стояк замерить до черновых работ.
4. К1-1 (П1 мойка кухонная): до Ст К1-1* 15,58 м через пом. 5, перепад 390 мм — короб 470×110 через чужие помещения не построить: насосная установка (КНС) у прибора, подиум или прибор ближе к стояку — решение К-11; до решения не выполнять.
5. Состав узла ввода В1, Т3 — по согласованию: на схеме типовой узел — кран шаровой, фильтр, счётчик, обратный клапан, кран; состав и места не определены (записи реестра нет). Доступ к арматуре — через люк не меньше 300×400. Водопровод — в штробе стен или в коробах; трубы испытать давлением до закрытия (акт скрытых работ).
6. Расчёт систем, диаметры магистралей и подбор оборудования выполняет проектная организация; врезка и перенос стояков — по согласованию с управляющей организацией. Арматуру и привязки сверить по паспортам приборов.
7. Ведомость выводов (код, прибор, высота, привязка) — лист 43; на схеме — только коды.
8. Ст К1-1*, Ст В1-1*, Ст Т3-1 на обмере не показаны: приняты рядом с Ст В1-1* (в МКД стоят группой) (К-4); положение сверить на объекте до разводки.
9. Знак «*» у стояка — положение принято, не замерено (все стояки); сверить на объекте до разметки. Реестр: листы 6–7, вопрос К-4.

Допущения и предложения на листе. Знак «*» принято (замерить). Знак «**» предложено (согласовать): дверь пом. 4 (стена Г). См. лист открытых вопросов (листы 6, 7).

Изм.	Кол.уч	Лист	№ док.	Подп.	Дата
Разраб.		Кырлан А.С.			13.11.26
Пров.					
ГИП					
Н. контр.					
Утв.					

ГД-2026-011-АИ

Квартира 56 м²

ЖК «Северный парк», Москва

Дизайн-проект интерьера

Стадия	Лист	Листов
РП	44	119

Схема разводки водопровода и канализации

М 1:200; 1:25

Кырлан Александр Сергеевич


выпуск 13.11.2026 № eb7810814f · стр. 49 из 139

Аксонометрическая схема В1 (холодное водоснабжение)

ПРЕДВАРИТЕЛЬНО · не для производства работ · открыто пунктов: 13 (реестр — л. 6, 7)

аксонометрия · диаметры, уклоны, отметки, стояки и приборы · трассы принципиальные

Схема В1 (М 1:50)

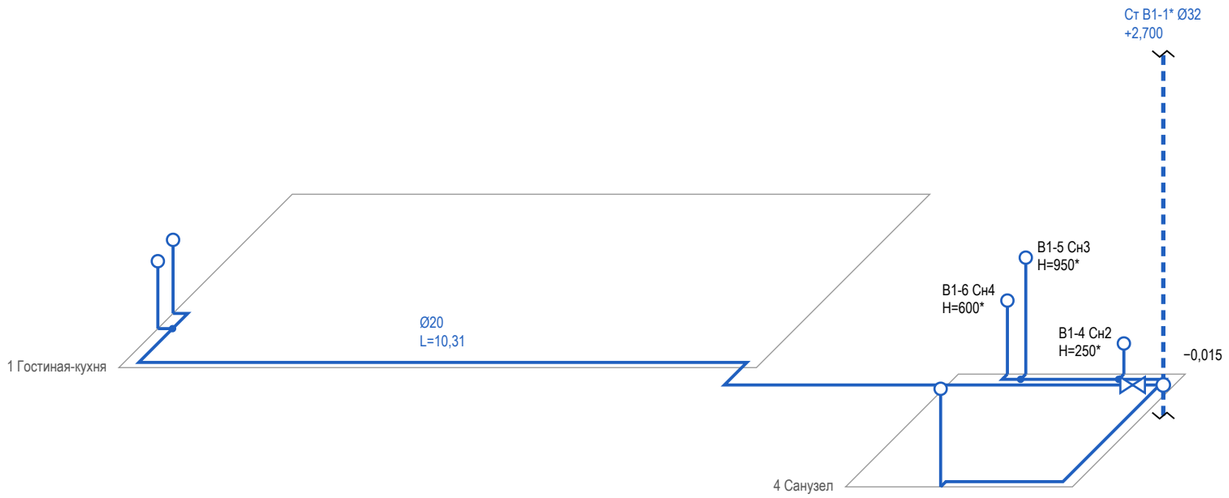

Ведомость выводов В1

Код	Прибор	H, мм	Ø, мм	Трасса, м
В1-1	П1 мойка кухонная	600*	20	10,31
В1-2	П2 посудомоечная машина	550*	20	0,12
В1-3	Сн1 ванна	800*	20	3,31
В1-6	Сн4 стиральная машина	600*	20	1,58
В1-5	Сн3 умывальник	950*	20	0,12
В1-4	Сн2 унитаз подвесной	250*	20	0,12

Условные обозначения

- В1 — водопровод хозяйственно-питьевой (ХВС), PP-R Ø20
- вывод В1 (код — в ведомости привязок)
- стояк «Ст К1-N / Ст В1-N» (ГОСТ 21.601), Ø мм
- стояк в плане (на отметке пола); вертикаль — стояк по высоте, разрыв — перекрытие
- тройник (ответвление к прибору)
- кран шаровой
- * стояк Т3 не на обмере — принят в шахте рядом со Ст В1, сверить

Примечания

1. Схема В1 построена по тем же трассам, что план разводки: положение в плане сохранено, глубина — в масштабе ×0,5. Трассы принципиальные; фактическое положение фиксируется исполнительной схемой до закрытия.
2. Высоты H — от чистого пола помещения, мм. Отметка прокладки магистрали В1 (в стяжке, в стене или по полу) в данных не задана: участки показаны на уровне пола условно (записи реестра нет).
3. * — высота вывода принята по практике монтажа; сверить по паспорту прибора.
4. Узел ввода В1 (кран, фильтр, счётчик, обратный клапан, кран) — на схеме разводки; состав узла ввода — по согласованию. Кран шаровой — на первом участке от стояка.
5. Ст В1-1* на обмере не показаны: положение принято (по брифу заказчика), не замерено (К-4); положение сверить на объекте до разводки.
6. Трубы испытать давлением до закрытия (акт скрытых работ, опрессовка по СП 73.13330.2016).
7. Диаметры, высоты выводов и места кранов — по паспортам выбранных приборов и расчёту проектной организации.
8. Расчёт систем, диаметры магистралей и подбор оборудования выполняет проектная организация.

1000 мм · печать 1:1

Допущения и предложения на листе. Знак «*» принято (замерить): Ст К1-1. См. лист открытых вопросов (листы 6, 7).

Изм.	Кол.уч	Лист	№ док.	Подп.	Дата
Разраб.		Кырлан А.С.			13.11.26
Пров.					
ГИП					
Н. контр.					
Утв.					

ГД-2026-011-АИ

Квартира 56 м²

ЖК «Северный парк», Москва

Дизайн-проект интерьера

Стадия	Лист	Листов
РП	45	119

Аксонометрическая схема В1 (холодное водоснабжение)

М 1:50

Кырлан Александр Сергеевич


выпуск 13.11.2026 № eb7810814f · стр. 50 из 139

Аксонометрическая схема Т3 (горячее водоснабжение)

ПРЕДВАРИТЕЛЬНО · не для производства работ · открыто пунктов: 13 (реестр — л. 6, 7)

аксонометрия · диаметры, уклоны, отметки, стояки и приборы · трассы принципиальные

Схема Т3 (М 1:50)

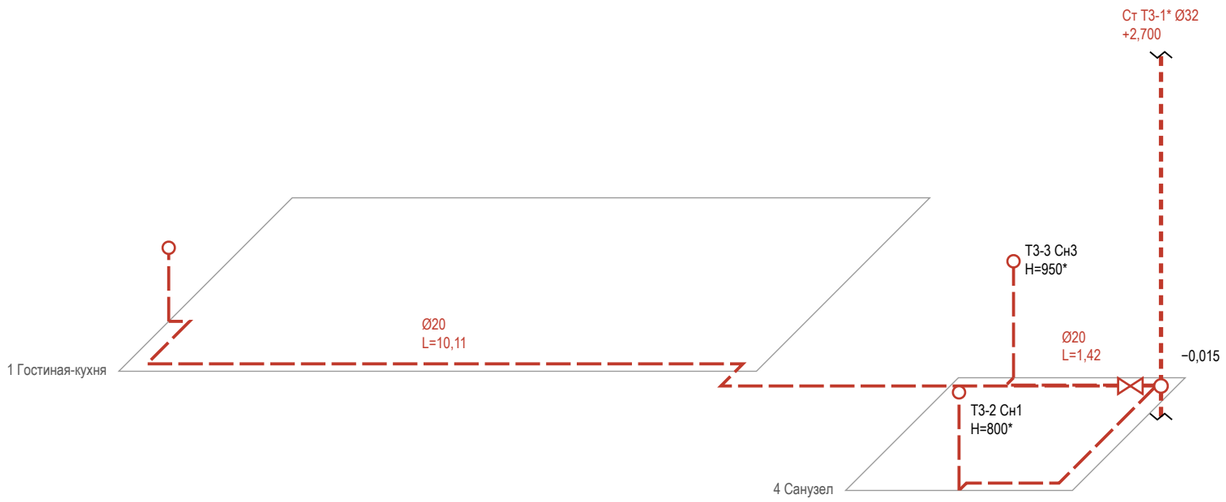

Ведомость выводов Т3

Код	Прибор	H, мм	Ø, мм	Трасса, м
Т3-1	П1 мойка кухонная	600*	20	10,11
Т3-2	Сн1 ванна	800*	20	3,17
Т3-3	Сн3 умывальник	950*	20	1,42

Условные обозначения

- Т3 — горячее водоснабжение, подача (ГВС), PP-R Ø20
- вывод Т3 (код — в ведомости привязок)
- стояк «Ст К1-N / Ст В1-N» (ГОСТ 21.601), Ø мм
- стояк в плане (на отметке пола); вертикаль — стояк по высоте, разрыв — перекрытие
- тройник (ответвление к прибору)
- кран шаровой
- * стояк Т3 не на обмере — принят в шахте рядом со Ст В1, сверить

Примечания

1. Схема Т3 построена по тем же трассам, что план разводки: положение в плане сохранено, глубина — в масштабе ×0,5. Трассы принципиальные; фактическое положение фиксируется исполнительной схемой до закрытия.
2. Высоты H — от чистого пола помещения, мм. Отметка прокладки магистрали Т3 (в стяжке, в стене или по полу) в данных не задана: участки показаны на уровне пола условно (записи реестра нет).
3. * — высота вывода принята по практике монтажа; сверить по паспорту прибора.
4. Узел ввода Т3 (кран, фильтр, счётчик, обратный клапан, кран) — на схеме разводки; состав узла ввода — по согласованию. Кран шаровой — на первом участке от стояка.
5. Циркуляция ГВС в данных не задана — циркуляционного трубопровода на схеме нет (записи реестра нет).
6. Ст Т3-1 на обмере не показаны: приняты рядом с Ст В1-1* (в МКД стоят группой); положение сверить на объекте до разводки.
7. Трубы испытать давлением до закрытия (акт скрытых работ, опрессовка по СП 73.13330.2016).
8. Диаметры, высоты выводов и места кранов — по паспортам выбранных приборов и расчёту проектной организации.
9. Расчёт систем, диаметры магистралей и подбор оборудования выполняет проектная организация.

1000 мм · печать 1:1

Допущения и предложения на листе. Знак «*» принято (замерить): Ст К1-1. См. лист открытых вопросов (листы 6, 7).

Изм.	Кол.уч	Лист	№ док.	Подп.	Дата
Разраб.		Кырлан А.С.			13.11.26
Пров.					
ГИП					
Н. контр.					
Утв.					

ГД-2026-011-АИ

Квартира 56 м²

ЖК «Северный парк», Москва

Дизайн-проект интерьера

Стадия	Лист	Листов
РП	46	119

Аксонометрическая схема Т3 (горячее водоснабжение)

М 1:50


Кырлан Александр Сергеевич

выпуск 13.11.2026 № eb7810814f · стр. 51 из 139

Аксонометрическая схема К1 (канализация)

аксонометрия · диаметры, уклоны, отметки, стояки и приборы · трассы принципиальные

Схема К1 (М 1:50)

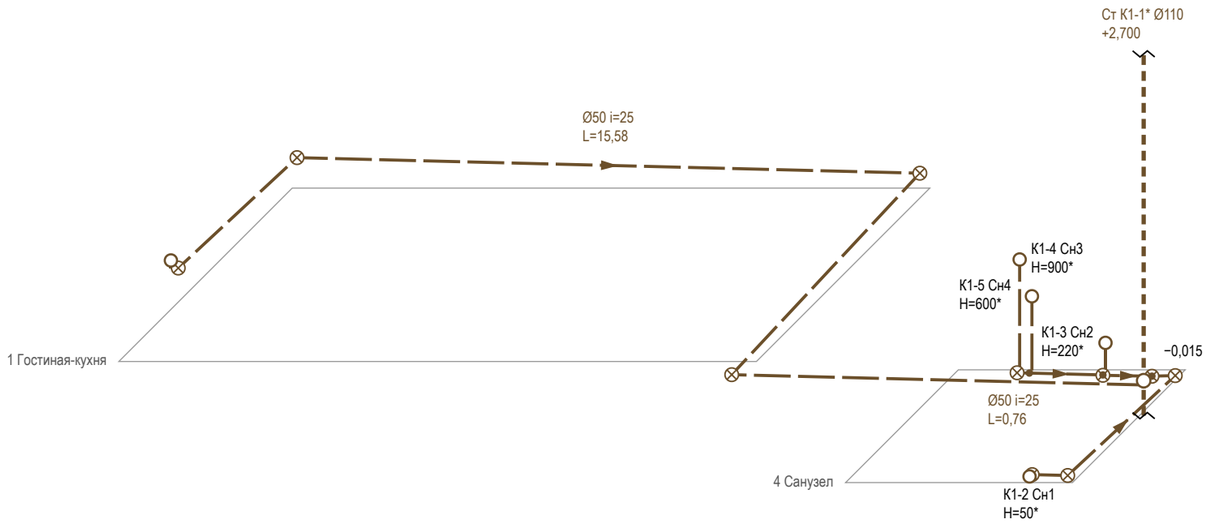

Ведомость выводов К1

Код	Прибор	H, мм	Ø, i	Трасса, м
К1-3	Сн2 унитаз подвесной	220*	110 i=20	0,65
К1-1	П1 мойка кухонная	400*	50 i=25	15,58
К1-2	Сн1 ванна	50*	50 i=25	3,02
К1-4	Сн3 умывальник	900*	50 i=25	0,76
К1-5	Сн4 стиральная машина	600*	50 i=25	0,06

Условные обозначения

- К1 — канализация бытовая
- вывод К1 (код — в ведомости привязок)
- стояк «Ст К1-N / Ст В1-N» (ГОСТ 21.601), Ø мм
- стояк в плане (на отметке пола); вертикаль — стояк по высоте, разрыв — перекрытие
- направление уклона К1 / пола: Ø, мм на 1 м
- ревизия (прочистка) К1 — доступ сохранить
- тройник (ответвление к прибору)
- * стояк Т3 не на обмере — принят в шахте рядом со Ст В1, сверить

Примечания

1. Схема К1 построена по тем же трассам, что план разводки: положение в плане сохранено, глубина — в масштабе ×0,5. Трассы принципиальные; фактическое положение фиксируется исполнительной схемой до закрытия.
2. Отметки — от плиты перекрытия: низ трубы у врезки в стояк — отметка из данных выпуска, к прибору труба поднимается на уклон i, мм/м (уклон не менее 1/d и не более 150 мм/м, СП 30.13330.2020, п. 19.1); чистый пол — выше плиты на стяжку (высота пирога пола). Высота выпуска прибора H — от чистого пола.
3. * — высота вывода принята по практике монтажа; сверить по паспорту прибора.
4. Ревизия — на повороте и в начале участка; стояк К1 в коробе с люком — звукоизоляция стояка в коробе; поворот — двумя отводами 45°.
5. Ст К1-1* на обмере не показаны: положение принято (по брифу заказчика), не замерено (К-4); положение сверить на объекте до разводки.
6. Трубы испытать давлением до закрытия (акт скрытых работ, опрессовка по СП 73.13330.2016).
7. Диаметры, высоты выводов и места кранов — по паспортам выбранных приборов и расчёту проектной организации.
8. Расчёт систем, диаметры магистралей и подбор оборудования выполняет проектная организация.

1000 мм · печать 1:1

Допущения и предложения на листе. Знак «*» принято (замерить): Ст В1-1. См. лист открытых вопросов (листы 6, 7).

Изм.	Кол.уч	Лист	№ док.	Подп.	Дата
Разраб.		Кырлан А.С.			13.11.26
Пров.					
ГИП					
Н. контр.					
Утв.					

ГД-2026-011-АИ

Квартира 56 м²

ЖК «Северный парк», Москва

Дизайн-проект интерьера

Стадия	Лист	Листов
РП	47	119

Аксонометрическая схема К1 (канализация)

М 1:50

Кырлан Александр Сергеевич


выпуск 13.11.2026 № eb7810814f · стр. 52 из 139

Развёртки мокрых зон: выводы ВК. Гостиная-кухня

пом. 1 · выводы В1, Т3, К1 на стенах · высоты от чистого пола, привязки от чистовых углов, мм

ПРЕДВАРИТЕЛЬНО · не для производства работ · открыто пунктов: 13 (реестр — л. 6, 7)

Стена Г (М 1:20)

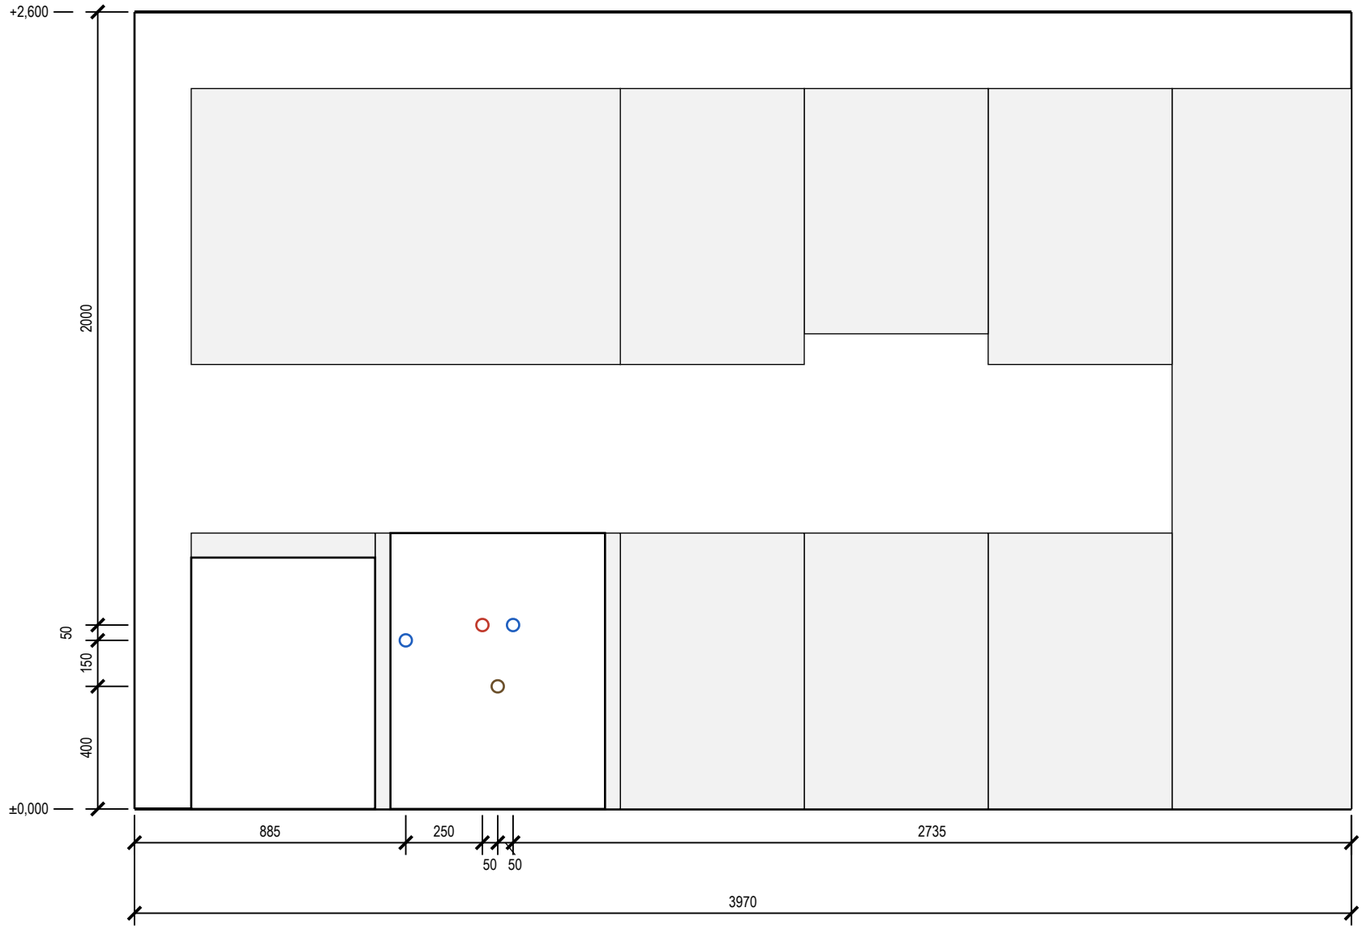

Допущения и предложения на листе

Основа листа: размеры помещений и положение проёмов введены заказчиком в брифе, на объекте не замерены (К-1); высота потолка 2700 мм — по брифу заказчика, не замерена (К-2); толщины стен приняты по брифу: наружные 200 мм, внутренние 150 мм — не обмерены (К-1); тип дома монолитный, перекрытие 200 мм — по брифу заказчика, документов нет (К-3); планировка (стены, проёмы, объединение кухни и гостиной, расширение санузла) — по брифу без обмера и плана БТИ (К-7); разрешённая мощность 10 кВт принята, ТУ не переданы (К-8); вентканалы приняты, в брифе не заданы (К-9); подрайон климата не задан — принят не северный (жилые от 2,5 м) (К-10).

См. лист открытых вопросов (лист 6, записи К-1–К-3, К-7–К-10).

Ведомость привязок выводов (от чистого пола и угла)

Код	Прибор	Ø	H, мм	Привязка, мм
В1-1	П1 мойка кухонная	½"	600*	ст. Г: 1235 от лев. угла
Т3-1	П1 мойка кухонная	½"	600*	ст. Г: 1135 от лев. угла
К1-1	П1 мойка кухонная	Ø50	400*	ст. Г: 1185 от лев. угла
В1-2	П2 посудомоечная машина	½"	550*	ст. Г: 885 от лев. угла

Условные обозначения

- вывод В1 (код — в ведомости привязок)
- вывод Т3 (код — в ведомости привязок)
- вывод К1 (код — в ведомости привязок)
- сантехприбор по расстановке (габарит модели)
- дверной проём; окно — сплошной контур

Примечания

1. Габариты и высоты приборов, межосевые смесителей и места кранов — по паспортам выбранных приборов, сверяются до разметки стен.
2. Высоты H — от чистого пола помещения, мм; отметка чистого пола и потолка — у левого края вида (от ±0,000 объекта). Привязки — от левого чистового угла вида (облицовка стен вычтена), как на развёртках стен.
3. * — высота принята по практике монтажа: в данных прибора её нет; до разметки стен сверить по паспорту выбранного прибора (смеситель, инсталляция, сифон).
4. Ревизионные люки к арматуре и ревизиям в данных не заданы: место и размер не определены (записи реестра нет).
5. Мойка, ПММ и фильтр — выводы в шкафу мойки; диаметры и положение сифона и кранов сверить по паспортам приборов и чертежам модуля.
6. Часть подписей выводов не уместилась у знака: коды и высоты — в ведомости привязок.
7. Расчёт систем водоснабжения и канализации и подбор оборудования выполняет проектная организация; лист задаёт места и высоты выводов.

1000 мм · печать 1:1

Изм.	Кол.уч	Лист	№ док.	Подп.	Дата
Разраб.		Кырлан А.С.			13.11.26
Пров.					
ГИП					
Н. контр.					
Утв.					

ГД-2026-011-АИ

Квартира 56 м²

ЖК «Северный парк», Москва

Дизайн-проект интерьера

Стадия	Лист	Листов
РП	48	119

Развёртки мокрых зон: выводы ВК. Гостиная-кухня

М 1:20

Кырлан Александр Сергеевич


выпуск 13.11.2026 № eb7810814f · стр. 53 из 139

Развёртки мокрых зон: выводы ВК. Санузел


пом. 4 · выводы В1, Т3, К1 на стенах · высоты от чистого пола, привязки от чистовых углов, мм

ПРЕДВАРИТЕЛЬНО · не для производства работ · открыто пунктов: 13 (реестр — л. 6, 7)

Стена А (М 1:25)

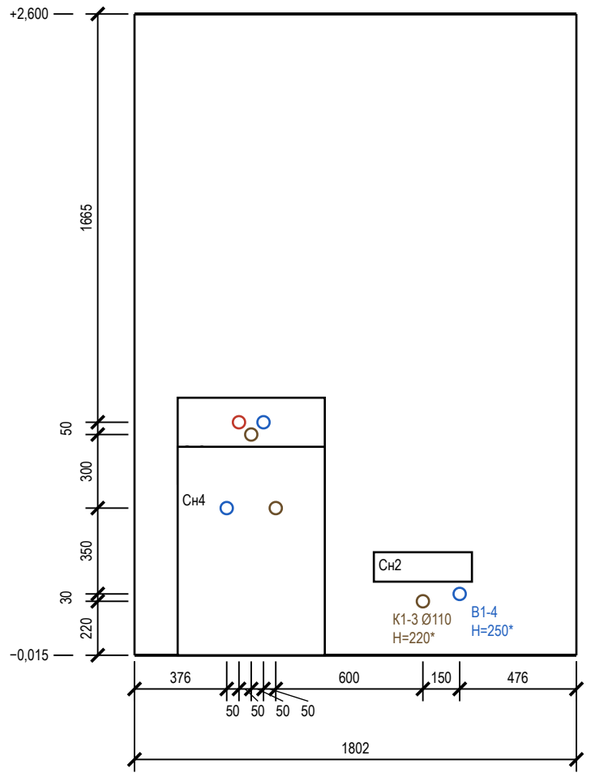

Стена В (М 1:25)

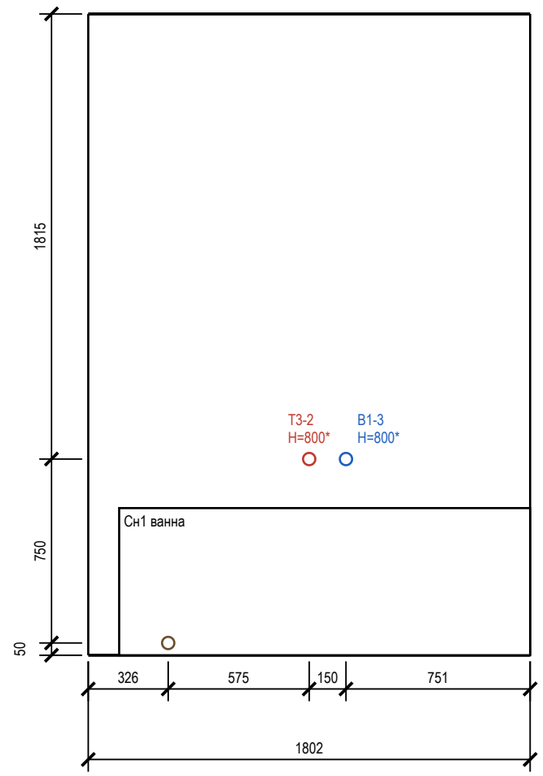

Допущения и предложения на листе

Основа листа: размеры помещений и положение проёмов введены заказчиком в брифе, на объекте не замерены (К-1); высота потолка 2700 мм — по брифу заказчика, не замерена (К-2); толщины стен приняты по брифу: наружные 200 мм, внутренние 150 мм — не обмерены (К-1); тип дома монолитный, перекрытие 200 мм — по брифу заказчика, документов нет (К-3); планировка (стены, проёмы, объединение кухни и гостиной, расширение санузла) — по брифу без обмера и плана БТИ (К-7); разрешённая мощность 10 кВт принята, ТУ не переданы (К-8); вентканалы приняты, в брифе не заданы (К-9); подрайон климата не задан — принят не северный (жилые от 2,5 м) (К-10).

Знак «*» — принято, не замерено и не подтверждено (замерить на объекте): К-4: Ст К1-1 — положение стояка канализации — по брифу заказчика, не замерено; Ст В1-1 — положение стояка холодной воды — по брифу заказчика, не замерено.

См. лист открытых вопросов (лист 6, записи К-1–К-4, К-7–К-10).

Ведомость привязок выводов (от чистого пола и угла)

Код	Прибор	Ø	H, мм	Привязка, мм
В1-4	Сн2 унитаз подвесной	½"	250*	ст. А: 1326 от лев. угла
К1-3	Сн2 унитаз подвесной	Ø110	220*	ст. А: 1176 от лев. угла
В1-5	Сн3 умывальник	½"	950*	ст. А: 526 от лев. угла
Т3-3	Сн3 умывальник	½"	950*	ст. А: 426 от лев. угла
К1-4	Сн3 умывальник	Ø50	900*	ст. А: 476 от лев. угла

Ведомость привязок (продолжение)

Код	Прибор	Ø	H, мм	Привязка, мм
В1-6	Сн4 стиральная машина	½"	600*	ст. А: 376 от лев. угла
К1-5	Сн4 стиральная машина	Ø50	600*	ст. А: 576 от лев. угла
В1-3	Сн1 ванна	½"	800*	ст. В: 1051 от лев. угла
Т3-2	Сн1 ванна	½"	800*	ст. В: 901 от лев. угла
К1-2	Сн1 ванна	Ø50	50*	ст. В: 326 от лев. угла

Условные обозначения

- вывод В1 (код — в ведомости привязок)
- вывод Т3 (код — в ведомости привязок)
- вывод К1 (код — в ведомости привязок)
- сантехприбор по расстановке (габарит модели)
- дверной проём; окно — сплошной контур

Примечания

1. Габариты и высоты приборов, межосевые смесителей и места кранов — по паспортам выбранных приборов, сверяются до разметки стен.
2. Высоты H — от чистого пола помещения, мм; отметка чистого пола и потолка — у левого края вида (от ±0,000 объекта). Привязки — от левого чистового угла вида (облицовка стен вычтена), как на развёртках стен.
3. * — высота принята по практике монтажа: в данных прибора её нет; до разметки стен сверить по паспорту выбранного прибора (смеситель, инсталляция, сифон).
4. Стояки в помещении: Ст К1-1* Ø110, Ст В1-1* Ø32, Ст Т3-1* Ø32 — положение на плане выводов; выводы подключаются к ним по схеме разводки.
5. Ревизионные люки к арматуре и ревизиям в данных не заданы: место и размер не определены (записи реестра нет).
6. Часть подписей выводов не уместилась у знака: коды и высоты — в ведомости привязок.
7. Стены Б, Г: выводов В1, Т3, К1 нет — развёртка не строится (иначе лист-продолжение); приборы и проёмы этих стен — на плане выводов и развёртках стен чертёжника.
8. Расчёт систем водоснабжения и канализации и подбор оборудования выполняет проектная организация; лист задаёт места и высоты выводов.

1000 мм · печать 1:1

Изм.	Кол.уч	Лист	№ док.	Подп.	Дата
Разраб.		Кырлан А.С.			13.11.26
Пров.					
ГИП					
Н. контр.					
Утв.					

ГД-2026-011-АИ

Квартира 56 м²

ЖК «Северный парк», Москва

Дизайн-проект интерьера

Стадия	Лист	Листов
РП	49	119

Развёртки мокрых зон: выводы ВК. Санузел

М 1:25

Кырлан Александр Сергеевич

выпуск 13.11.2026 № eb78108814f · стр. 54 из 139

Спецификация сантехнического оборудования

Форма 1 ГОСТ 21.110-2013 · ГД-2026-011-АИ-ВК.СО · приборы, арматура, трубопроводы

ПРЕДВАРИТЕЛЬНО · не для производства работ · открыто пунктов: 13 (реестр — л. 6, 7)

Поз.	Наименование и техническая характеристика	Тип, марка, обозначение документа	Код продукции	Поставщик	Ед. изм.	Кол.	Масса 1 ед., кг	Примечание
	Санитарные приборы							
1	Ванна встраиваемая акриловая 1700×750 мм, с каркасом, экраном и отверстием слив-перелив	акриловая 1700×750, смеситель настенный		выбор заказчика	шт	1		Сн1
2	Унитаз подвесной безободковый, с сиденьем микролифт, крепёж и звукоизолирующая прокладка	Laufen Pro 8.2096.6.000.000.1		выбор заказчика	шт	1		Сн2
3	Инсталляция для подвесного унитаза: рама высотой 1120 мм, бачок, клавиша смыва (ось клавиши 1050 мм от чистого пола)	аналог		выбор заказчика	шт	1		Сн2; короб ГКЛВ
4	Раковина над стиральной машиной 600×450 мм, плоская, с переливом и выпуском под плоский сифон	аналог		выбор заказчика	шт	1		Сн3
5	Мойка врезная, нержавеющая сталь, чёрная 700×480 мм, с переливом	аналог		с кухонной мебелью	шт	1		П1
6	Полотенцесушитель электрический, IP44, с терморегулятором	аналог		выбор заказчика	шт	1		Сн5
	Смесители, сифоны и арматура приборов							
7	Смеситель для ванны настенный однорычажный, межосевое 150 мм, с душевым набором (лейка, шланг, держатель)	аналог		выбор заказчика	шт	1		Сн1
8	Смеситель для умывальника однорычажный, с донным клапаном	аналог		выбор заказчика	шт	1		Сн3
9	Смеситель кухонный однорычажный, высокий излив	аналог		выбор заказчика	шт	1		П1
10	Обвязка ванны слив-перелив Ø40/50 с сифоном	аналог		выбор заказчика	шт	1		Сн1
11	Сифон плоский для раковины над стиральной машиной Ø32/40–50, выпуск в стену над корпусом машины	аналог		выбор заказчика	шт	1		Сн3
12	Сифон для мойки с отводом для ПММ Ø40/50	аналог		выбор заказчика	шт	1		П1; слив П2
13	Сифон для стиральной машины встраиваемый в стену Ø50, с обратным клапаном	аналог		выбор заказчика	шт	1		Сн4
14	Кран угловой ½"×½" с гибкой подводкой 40 см (умывальники, мойка)	аналог		выбор заказчика	шт	4		по 2 на прибор
15	Кран шаровой угловой ½"×¾" для подключения стиральной и посудомоечной машины	аналог		выбор заказчика	шт	2		Сн4, П2
	Трубопроводы							
16	Труба полипропиленовая PP-R PN20 Ø20×3,4 (В1)	ГОСТ 32415-2013		выбор заказчика	м	21,5	0,17	15,6 + 3,8 + 10 %
17	Труба PP-R, армированная стекловолокном, PN20 Ø20×2,8 (Т3)	ГОСТ 32415-2013		выбор заказчика	м	19	0,15	14,7 + 2,4 + 10 %
18	Труба канализационная ПП Ø50 (К1)	ГОСТ 32414-2013		выбор заказчика	м	24		19,4 + 1,9 + 10 %
19	Труба канализационная ПП Ø110 (К1)	ГОСТ 32414-2013		выбор заказчика	м	1		0,7 + 0,2 + 10 %
	Фасонные части и выводы							
20	Отвод канализационный ПП 45° Ø50	ГОСТ 32414-2013		выбор заказчика	шт	16		2 шт. на поворот
21	Отвод канализационный ПП 45° Ø110	ГОСТ 32414-2013		выбор заказчика	шт	4		2 шт. на поворот
22	Тройник канализационный ПП 45° (врезки ветвей)	ГОСТ 32414-2013		выбор заказчика	шт	4		
23	Ревизия канализационная ПП (после поворота трассы)	ГОСТ 32414-2013		выбор заказчика	шт	6		доступ сохранить
24	Фитинги PP-R Ø20: тройники, угольники 90° (ветви и повороты В1, Т3)	ГОСТ 32415-2013		выбор заказчика	шт	23		
25	Водорозетка PP-R Ø20×½" настенная, с креплением	ГОСТ 32415-2013		выбор заказчика	шт	9		коды — лист выводов
	Узлы ввода, люки, короба							
26	Кран шаровой латунный Ду15 PN16 (отключение ввода)	аналог		выбор заказчика	шт	2		Ст В1-1*, Ст Т3-1*
27	Фильтр сетчатый косой Ду15	аналог		выбор заказчика	шт	2		
28	Счётчик воды крыльчатый Ду15 (ХВ, ГВ), с поверкой	аналог		выбор заказчика	шт	2		пломба УК
29	Клапан обратный Ду15	аналог		выбор заказчика	шт	2		
30	Люк ревизионный нажимной под плитку 300×400 мм	аналог		выбор заказчика	шт	1		к стоякам и арматуре
31	Звукоизоляция стояка К1 в коробе: рулонный звукоизоляционный материал ≥ 10 мм, обмотка стояка на высоту этажа	аналог		выбор заказчика	м	2,7		Ст К1-1*
32	Короб К1 над полом: профиль ПН/ПС, ГКЛВ 12,5 мм под плитку	аналог		выбор заказчика	м	9,7		сечение — лист разводки

Примечания

1. Форма 1 ГОСТ 21.110-2013, ширины граф изменены по п. 4.1. «Аналог» — аналог по характеристикам: модели внести до черновых работ, привязки выводов сверить по паспортам.
2. Бытовая техника не входит (показана арматура подключения), мойка — в комплекте кухни (марка — модуля кухни, как у столяра). Длины труб — трасса листа разводки + подъёмы + 10 %.
3. Стояк К1 в коробе — звукоизоляция стояка в коробе без жёсткого контакта короба с трубой. Стояки со «*» (Ст К1-1*, Ст В1-1*, Ст Т3-1) приняты положение и число узлов ввода сверить на объекте.
4. Расчёт систем водоснабжения и канализации, диаметры магистралей и подбор оборудования выполняет проектная организация.

Допущения и предложения на листе

Основа листа: размеры помещений и положение проёмов введены заказчиком в брифе, на объекте не замерены (К-1); высота потолка 2700 мм — по брифу заказчика, не замерена (К-2); толщины стен приняты по брифу: наружные 200 мм, внутренние 150 мм — не обмерены (К-1); тип дома монолитный, перекрытие 200 мм — по брифу заказчика, документов нет (К-3); планировка (стены, проёмы, объединение кухни и гостиной, расширение санузла) — по брифу без обмера и плана БТИ (К-7); разрешённая мощность 10 кВт принята, ТУ не переданы (К-8); вентканалы приняты, в брифе не заданы (К-9); подрайон климата не задан — принят не северный (жилые от 2,5 м) (К-10).
Знак «*» — принято, не замерено и не подтверждено (замерить на объекте): К-4: Ст К1-1 — положение стояка канализации — по брифу заказчика, не замерено; Ст В1-1 — положение стояка холодной воды — по брифу заказчика, не замерено.
См. лист открытых вопросов (лист 6, записи К-1–К-4, К-7–К-10).

Изм.	Кол.уч	Лист	№ док.	Подп.	Дата
Разраб.		Кырлан А.С.			13.11.26
Пров.					
ГИП					
Н. контр.					
Утв.					

ГД-2026-011-АИ

Квартира 56 м²

ЖК «Северный парк», Москва

Дизайн-проект интерьера

Стадия	Лист	Листов
РП	50	119

Спецификация сантехнического оборудования

М б/м

Кырлан Александр Сергеевич

выпуск 13.11.2026 № eb7810814f · стр. 55 из 139

Техническое задание на подбор светильников

ПРЕДВАРИТЕЛЬНО · не для производства работ · открыто пунктов: 13 (реестр — л. 6, 7)

Параметры для подбора: светильники, ленты и блоки питания, слои света, сценарии помещений со светорегуляторами · б/м

Параметры светильников для подбора

Поз.	Марки	Наименование	Установка	Кол.	P, Вт	Σ P, Вт	Ф, лм	Тц, К	Ra	Угол, °	IP	Дим.	Слой	Группа	Пом.
1	Св31**, Св32**, Св33**, Св34**, Св35**, Св36**, Св37**, Св38**	Встраиваемый точечный	в ГКЛ, корпус ≤ 70 мм	8	12	96	1000	3000	90	—	20	да	общий	L12	1
2	Св41	Лента светодиодная 24 В	в нише уровня, профиль с рассеивателем	6,4 м	9,6/м	61,4	900/м	2700	90	—	20	да	акцентный	L13	1
3	Св42**, Св43**, Св44**	Подвесной	подвес, низ H=1450	3	9	27	800	3000	90	—	20	да	общий	L14	1
4	Св45–Св48	Встраиваемый точечный	в ГКЛ, корпус ≤ 70 мм	4	10	40	900	3000	90	—	20	—	общий	L15	1
5	Св49**	Линейный настенный	под верхними шкафами, H=1440	1	18	18	1500	3000	90	—	20	да	рабочий	L16	1
6	Св1–Св8	Встраиваемый точечный	в ГКЛ, корпус ≤ 70 мм	8	12	96	1000	2700	90	—	20	—	общий	L1	2
7	Св9	Лента светодиодная 24 В	в карнизе короба, профиль с рассеивателем	11,7 м	9,6/м	112,3	900/м	2700	90	—	20	да	акцентный	L2	2
8	Св10, Св11, Св24, Св25	Настенный (бра)	на стене, H=1500	4	6	24	400	2700	90	60	20	—	рабочий	L3, L9	2, 3
9	Св17–Св22	Встраиваемый точечный	в ГКЛ, корпус ≤ 70 мм	6	12	72	1050	2700	90	—	20	—	общий	L7	3
10	Св23	Лента светодиодная 24 В	в карнизе короба, профиль с рассеивателем	8,7 м	9,6/м	83,5	900/м	2700	90	—	20	да	акцентный	L8	3
11	Св12–Св14	Встраиваемый точечный	в ГКЛ, корпус ≤ 70 мм	3	6	18	500	3000	90	—	44	—	общий	L4	4
12	Св15**	Настенный светильник над зеркалом, драйвер встроен	над зеркалом, H=1900	1	8	8	600	3000	90	—	44	—	рабочий	L5	4
13	Св26–Св29	Встраиваемый точечный	в ГКЛ, корпус ≤ 70 мм	4	7	28	600	3000	90	—	20	—	общий	L10	5
14	Св30**	Лента светодиодная 24 В	на поверхности, профиль с рассеивателем, датчик движения	1,8 м	4,8/м	8,6	150/м	2700	90	—	20	нет	ночной	L11	5
		Итого		**42 шт + 28,6 м**		**692,9**									

Слои света по помещениям

Пом.	Помещение	Слои света — группы включения (марки — в спецификации)	Σ P, Вт
1	Гостиная-кухня	общий — L12, L14, L15; рабочий — L16; акцентный — L13	242,4
2	Спальня	общий — L1; рабочий — L3; акцентный — L2	220,3
3	Детская	общий — L7; рабочий — L9; акцентный — L8	167,5
4	Санузел	общий — L4; рабочий — L5	26
5	Прихожая	общий — L10; ночной — L11	36,6

LED-ленты, линейные светильники и блоки питания

Марка	Пом.	L, м	U, В	Вт/м	Σ P, Вт	БП	P БП, Вт	Загр., %	Питание	Доступ к БП
Св41	1	6,4	24	9,6	61,4	БП4	300	20	с двух концов	люк 300×300 в нише фигуры потолка ПТ1
Св49**	1	3	24	—	18	БП5**	60	30	встроенный ввод	в колонне Кх1 над нишей холодильника, верх, съёмная панель
Св9	2	11,7	24	9,6	112,3	БП1	200	56	с двух концов	люк 300×300 в коробе потолка ПТ1
Св23	3	8,7	24	9,6	83,5	БП2	200	42	с двух концов	люк 300×300 в коробе потолка ПТ1
Св30**	5	1,8	24	4,8	8,6	БП3	20	43	с одного конца	в шкафу Пр1, верхняя полка

Сценарии (помещения со светорегуляторами)

Помещение	Сценарий	Горят группы (уровень)	Управление
1. Гостиная-кухня	Вечер	L12 споты гостиной — 30 %; L13 подсветка короба — 100 %; L14 подвесы над столом — 50 %; остальные выкл.	светорегуляторы S7, S8**, S12**
	Ужин	L13 подсветка короба — 60 %; L14 подвесы над столом — 100 %; L16 подсветка столешницы — 30 %; остальные выкл.	светорегуляторы S8**, S9**, S12**
	Кино	L13 подсветка короба — 20 %; остальные выкл.	светорегулятор S12**
	Готовка	L12 споты гостиной — 50 %; L15 споты кухни — вкл.; L16 подсветка столешницы — 100 %; остальные выкл.	светорегуляторы S7, S9**; выключатель S13**

Слои света

общий — равномерный свет помещения, по норме освещённости

рабочий — местный свет задачи: столешница, зеркало, чтение у кровати

акцентный — подсветка потолка, стен и ниш; не входит в поток общего света

ночной — путь спальня → санузел: не выше 2700 K, малая яркость, датчик движения

Допущения и предложения на листе

Основа листа: размеры помещений и положение проёмов введены заказчиком в брифе, на объекте не замерены (К-1); высота потолка 2700 мм — по брифу заказчика, не замерена (К-2); толщины стен приняты по брифу: наружные 200 мм, внутренние 150 мм — не обмерены (К-1); тип дома монолитный, перекрытие 200 мм — по брифу заказчика, документов нет (К-3); планировка (стены, проёмы, объединение кухни и гостиной, расширение санузла) — по брифу без обмера и плана БТИ (К-7); разрешённая мощность 10 кВт принята, ТУ не переданы (К-8); вентканалы приняты, в брифе не заданы (К-9); подрайон климата не задан — принят не северный (жилые от 2,5 м) (К-10).

Знак «**» — предложение проектировщика, заказчиком не утверждено (согласовать с заказчиком): S12 — свой пост группе L13: сценарии «Вечер», «Ужин», «Кино», «Готовка» включают её отдельно от L12 — на одном светорегуляторе не набрать; S8, S9 — светорегулятор добавлен разработчиком проекта; S13 — свой пост группе L15: сценарии «Вечер», «Ужин», «Готовка» включают её отдельно от L14 — на одном светорегуляторе не набрать; Св31, Св32, Св33, Св34, Св35, Св36, Св37, Св38 — ряды — по зоне гостиной (по мебели); Св42, Св43, Св44, Св49, БП5 — диммируемость добавлена разработчиком проекта под светорегуляторы S8 и S9; Св15 — Сдвиг под раскладку плитки стены А на 52 мм вдоль стены — ось на шве или в центре плитки, привязка по таблице листа; Св30 — открытая лента в накладном профиле вместо «в коробе»: короба в потолке нет — подвесной потолок помещения без короба и ниши LED.

См. лист открытых вопросов (лист 6, записи К-1–К-3, К-7–К-10).

Примечания

1. Позиции и марки Св — те же, что на плане освещения (лист 33) и в ведомости светильников (лист 35); группы L — по плану выключателей (лист 34).
2. Модели светильников не выбраны: лист — техническое задание на подбор. Модель по строке таблицы: поток, Тц, Ra, угол, IP и регулировка яркости не хуже указанных, мощность не больше; встраиваемые — под глубину короба (графа «Установка»). IP 20 — сухие помещения. После выбора моделей (артикул, производитель) лист выпускается как «Спецификация светильников».
3. Длина LED-ленты в карнизе и нише уровня — по линиям карниза и ниши плана потолков (лист 53); Σ P = Вт/м × длина. Блок питания загружен не больше чем на 80 %; лента 24 В длиннее 10 м питается с двух концов; доступ к блоку питания — люк ревизии 300×300 мм или место, указанное в таблице.
4. Сценарии: % — яркость группы на светорегуляторе; «вкл.» — группа на обычной клавише; группы, не названные в строке, выключены. Светильники и блоки питания групп на светорегуляторе — с регулировкой яркости. Клавиши и светорегуляторы — лист 34.
5. В пом. 2, 3 свет включается клавишами групп — лист 34.
6. Мощность и поток в таблице — требования к подбору (поток не меньше, мощность не больше указанных); после выбора модели — по её паспорту, Σ P — установленная мощность освещения. Оценка освещённости — на плане освещения; это не светотехнический расчёт.

Изм.	Кол.уч	Лист	№ док.	Подп.	Дата
Разраб.		Кырлан А.С.			13.11.26
Пров.					
ГИП					
Н. контр.					
Утв.					

ГД-2026-011-АИ

Квартира 56 м²

ЖК «Северный парк», Москва

Дизайн-проект интерьера

Стадия	Лист	Листов
РП	51	119

Техническое задание на подбор светильников

М б/м

Кырлан Александр Сергеевич


выпуск 13.11.2026 № eb7810814f · стр. 56 из 139

Схема каркаса перегородки П-2

С112; вид, сечения и узлы: каркас, обрамление проёма и примыкания

ПРЕДВАРИТЕЛЬНО · не для производства работ · открыто пунктов: 13 (реестр — л. 6, 7)


Вид на каркас без обшивки (М 1:25)

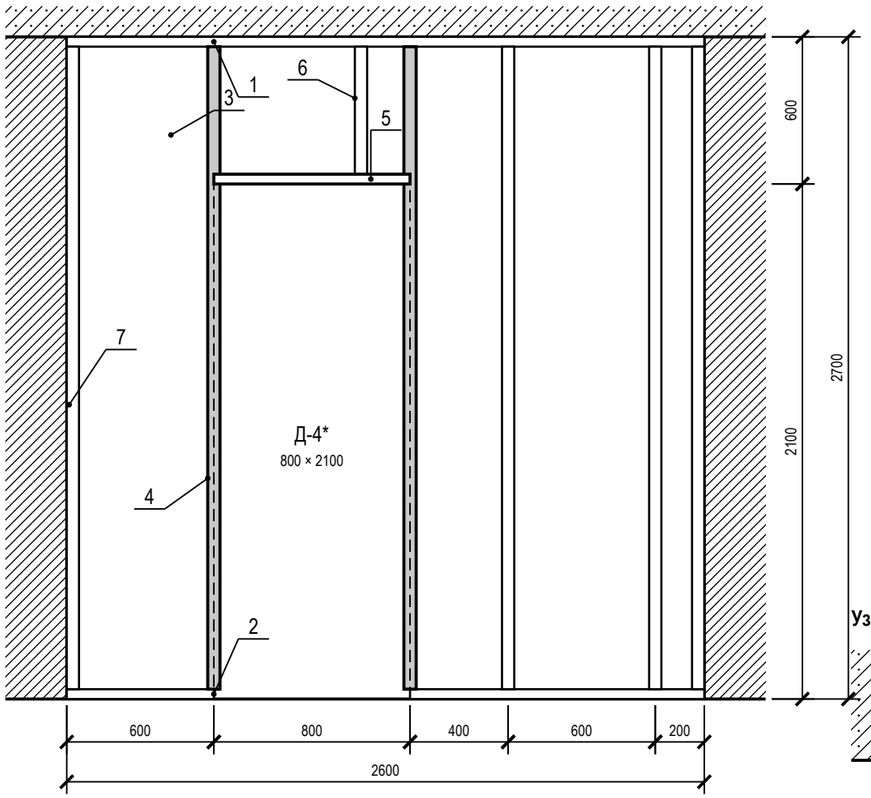

Оси — стойки каркаса; полки профиля на виде условны

Сечение А–А по стойке (М 1:5)


сверху — пом. 3, окраска

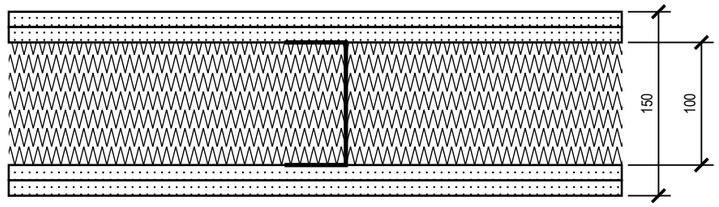

снизу — пом. 5, окраска

поз. 9 — ГКЛ 12,5 мм в 2 слоя с каждой стороны; поз. 3 — ПС 100; поз. 8 — минвата 100 мм (принято)

Сечение Б–Б у проёма, на уровне ниже перемычки (М 1:5)

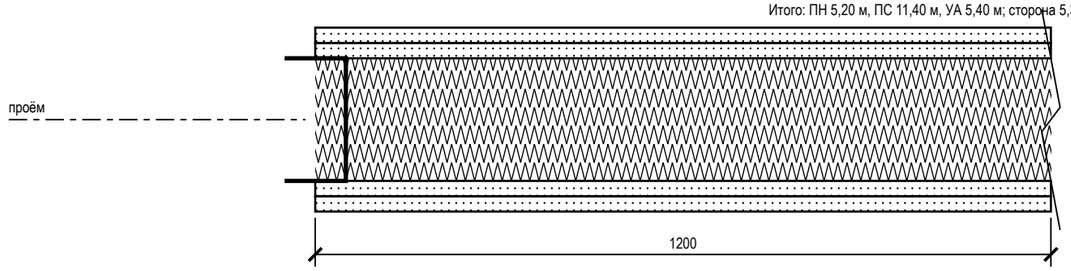


поз. 4 — УА 100, обрамление проёма; обшивка по краю проёма, простенок 1200 мм до пилона (на сечении показан с обрывом)

Ведомость элементов каркаса


Поз.	Наименование	Кол-во	Ед.
1	ПН 100 по потолку (к перекрытию)	2,60	м
2	ПН 100 по полу, без проёма	1,80	м
3	ПС 100 через 600 мм	4 × 2,70	м
4	УА 100 по краям проёма	2 × 2,70	м
5	ПН 100 перемычка над проёмом	0,80	м
6	ПС 100 над перемычкой	1 × 0,60	м
7	Лента уплотнительная под профили	9,80	м
8	Минвата в полость, 100 мм	5,34	м²
9	ГКЛ 12,5 мм, 2 слоя с двух сторон	21,36	м²

Итого: ПН 5,20 м, ПС 11,40 м, УА 5,40 м; сторона 5,34 м²

Узел 1. К плите (М 1:5)

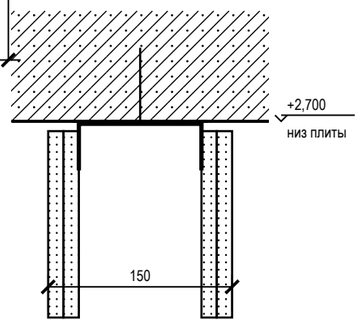

Узел 2. К полу (М 1:5)

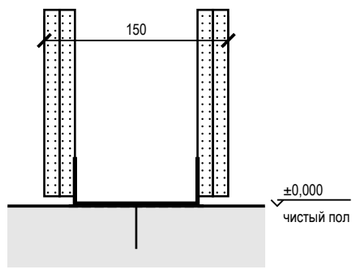

Примечания

1. П-2** (С112, ГКЛ в 2 слоя с каждой стороны, толщина 150 мм, высота 2700 мм до плиты) — предложение проектировщика, автором не утверждено (К-5); ось и длина 2600 мм — со скана плана заказчика (контрольный обмер не выполнялся).
2. Шаг стоек 600 мм — по данным (под плитку и во влажной зоне). Размеры сечений профилей — «ПС 100», «УА 100» по данным и каталогу; толщины листов — ГОСТ 32614-2012.
3. Принято: шаг стоек 600 мм принят по базовому правилу: в проекте шаг не задан.
4. Принято: проём Д-4 в каркасе 800 × 2100 мм принят по размеру полотна: короб скрытой двери (модель, размеры) не выбран — проём пересчитать по коробке до монтажа УА (К-5).
5. Принято: перемычка над проёмом — направляющий профиль по верху проёма на всю его ширину; короткие стойки ПС над перемычкой на шаге каркаса: по практике узла Knauf, не по данным объекта (К-5).
6. Принято: заполнение полости — минераловатная плита на всю глубину профиля (Rw системы С112 нормируют с заполнением); марка и плотность выбираются при закупке (К-5).
7. Принято: длина стойки равна высоте перегородки: стойки режут на высоту между направляющими при монтаже, зазоры до плиты и пола в проекте не заданы.
8. Обшивку крепят к стойкам шурупами через слой, швы слоёв вразбежку; зазоры обшивки до плиты и пола, шаг дюбелей, марка заполнения — по ТУ системы и узлу изготовителя.

Допущения и предложения на листе

Основа листа: размеры помещений и положение проёмов введены заказчиком в брифе, на объекте не замерены (К-1); высота потолка 2700 мм — по брифу заказчика, не замерена (К-2); толщины стен приняты по брифу: наружные 200 мм, внутренние 150 мм — не обмерены (К-1); тип дома монолитный, перекрытие 200 мм — по брифу заказчика, документов нет (К-3); планировка (стены, проёмы, объединение кухни и гостиной, расширение санузла) — по брифу без обмера и плана БТИ (К-7); разрешённая мощность 10 кВт принята, ТУ не переданы (К-8); вентканалы приняты, в брифе не заданы (К-9); подрайон климата не задан — принят не северный (жилые от 2,5 м) (К-10).

Знак «**» — предложение проектировщика, заказчиком не утверждено (согласовать с заказчиком): К-5: П-2 — положение, материал (ГКЛ) и толщина 150 мм — по брифу заказчика; конструкция (система С112, 2 слоя с каждой стороны, Rw 51 дБ — нижняя граница диапазона системы С112 (51–56 дБ)) — выбор исполнителя, автором не утверждена.

См. лист открытых вопросов (лист 6, записи К-1–К-3, К-5, К-7–К-10).

Изм.	Кол.уч	Лист	№ док.	Подп.	Дата
Разраб.		Кырлан А.С.			13.11.26
Пров.					
ГИП					
Н. контр.					
Утв.					

ГД-2026-011-АИ

Квартира 56 м²

ЖК «Северный парк», Москва

Дизайн-проект интерьера

Стадия	Лист	Листов
РП	52	119

Схема каркаса перегородки П-2

М 1:25; 1:5

Кырлан Александр Сергеевич

выпуск 13.11.2026 № eb7810814f · стр. 57 из 139

06

Потолки и ГКЛ-конструкции


Кырлан Александр Сергеевич

выпуск 13.11.2026 · eb78110814f · стр. 58 из 139

План потолков

Уровни и марки потолков, короба с подсветкой, ниши под шторы, люки, вырезы · отметки низа от ±0,000 чистого пола · размеры в мм

ПРЕДВАРИТЕЛЬНО · не для производства работ · открыто пунктов: 13 (реестр — л. 6, 7)

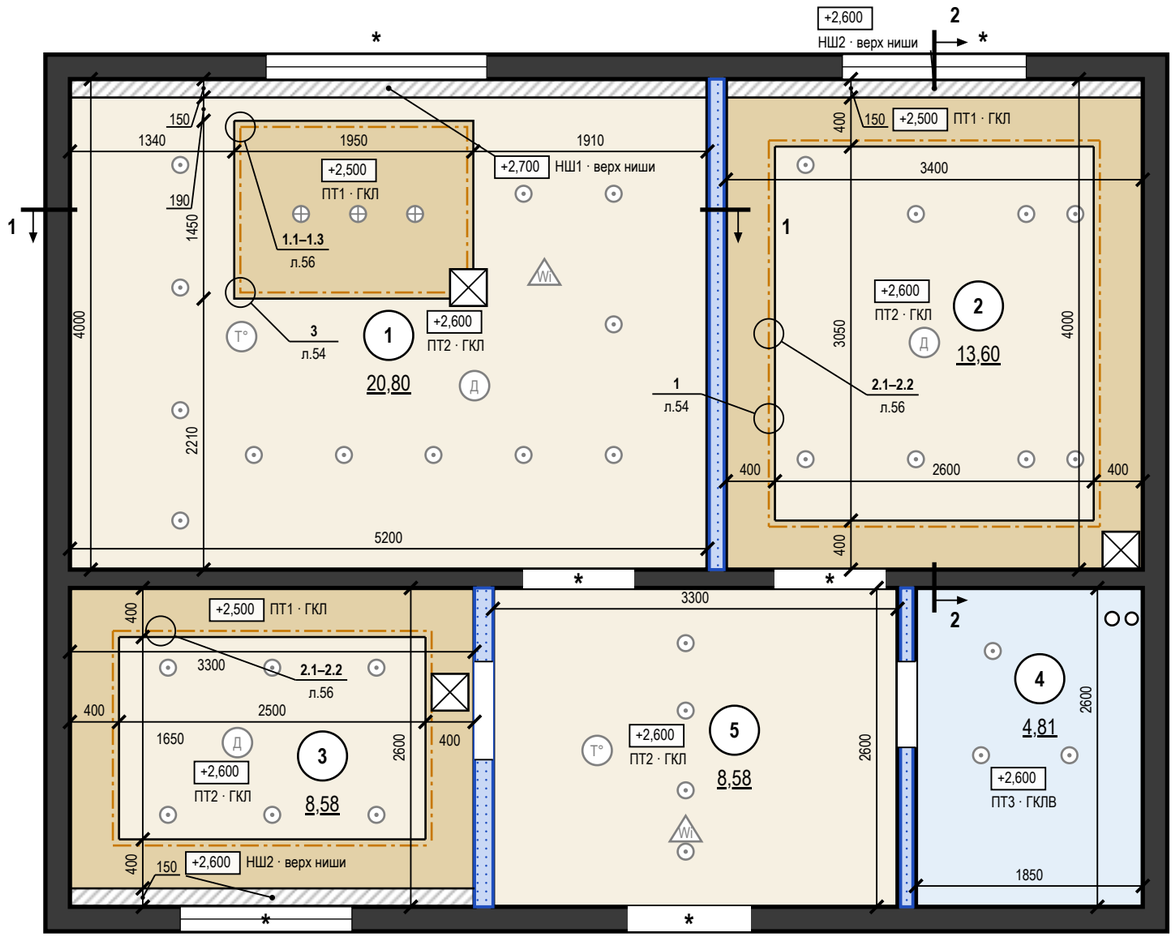

Ведомость потолков

Пом.	Марка	Конструкция	Низ / верх ниши	S, м²	Q
1	ПТ1	ГКЛ П113, остров + LED	+2,500	2,83	Q3
1	ПТ2	ГКЛ П113	+2,600	17,19	Q3
1	НШ1	ниша под шторы 150×100	+2,700	0,78	
2	ПТ1	ГКЛ П113, короб LED	+2,500	5,16	Q3
2	ПТ2	ГКЛ П113	+2,600	7,93	Q3
2	НШ2	ниша под шторы 150×100	+2,600	0,51	
3	ПТ1	ГКЛ П113, короб LED	+2,500	3,96	Q3
3	ПТ2	ГКЛ П113	+2,600	4,13	Q3
3	НШ2	ниша под шторы 150×100	+2,600	0,49	
4	ПТ3	ГКЛВ П113	+2,600	4,81	Q3
5	ПТ2	ГКЛ П113	+2,600	8,58	Q3
		Итого		**56,37**	

Ведомость вырезов и закладных в потолке

Марка	Устройство	Кол.	Пом.
	Светильник встраиваемый (марки — план освещения)	33	1, 2, 3, 4, 5
	Светильник подвесной (марки — план освещения)	3	1
ИП4, ИП1, ИП2	Извещатель дымовой	3	1, 2, 3
ИП5, ИП3	Извещатель тепловой	2	1, 5
АР2**, АР1**	Точка доступа Wi-Fi, PoE	2	1, 5
	Люк ревизии 300×300	3	1, 2, 3

Условные обозначения

- ПТ1 — ГКЛ по каркасу П113, низ +2,500
- ПТ2 — ГКЛ по каркасу П113, низ +2,600
- ПТ3 — ГКЛВ по каркасу П113, низ +2,600
- НШ1 — ниша под шторы 150×100, верх +2,700
- НШ2 — ниша под шторы 150×100, верх +2,600
- граница уровней потолка (перепад)
- LED-лента в нише подсветки (карниз короба, ниша фигуры)
- стояк: К1 — канализация, В1 — ХВС, Т3 — ГВС
- люк ревизии в потолке 300×300 мм (доступ к БП LED)
- светильник встраиваемый — подложка с плана освещения
- светильник подвесной — подложка с плана освещения

Условные обозначения (продолжение)

- Д — извещатель дымовой на потолке — подложка
- Т° — извещатель тепловой на потолке — подложка
- Wi — точка доступа Wi-Fi на потолке — подложка
- линия разреза у стен помещения, стрелка — направление взгляда
- место узла и сечений М 1:10: номер узла или сечений на полке, под полкой — лист
- +2,600 — отметка низа потолка, м (у ниши под шторы — верх ниши); под ней марка потолка
- новое — возводится по проекту (синим)
- 1 — номер помещения, площадь м²

Допущения и предложения на листе. Знак «*» принято (замерить): Ст К1-1, Ст В1-1. Знак «**» предложено (согласовать): П-1, П-2, П-3. См. лист открытых вопросов (листы 6, 7).

Примечания

1. За отметку ±0,000 принят уровень чистого пола сухих помещений (готовое покрытие), а не существующего пола; пол пом. 4 — −0,015; верх плиты перекрытия −0,064 — расчётный по пирогу пола, не замерен; существующий пол снимается до плиты, его отметка не замерена. Отметки в прямоугольниках — низ потолка; низ плиты +2,700. Марка потолка — одна конструкция и отметка на весь альбом.
2. Потолки ГКЛ — каркасная система П113: подвесы через 1000 (с запасом: СП 163, табл. 14 — до 1100 при 0,15 кН/м²), несущие профили через 500, основные через 1200 мм; листы — поперёк несущих профилей. В помещениях 4 — ГКЛВ на оцинкованном каркасе.
3. Нижний уровень — пояс-короб по периметру шириной 400 мм, верхний — поле внутри пояса: пом. 2, 3.
4. LED-лента в алюминиевом профиле посередине карниза короба шириной 400 мм (узел 1, лист 54); длина по плану: пом. 2 — 11,7 м (в плане освещения 11,7); пом. 3 — 8,7 м (в плане освещения 8,7).
5. Ниши под шторы 150×100 мм — на всю длину стены с окном; карниз — на закладной до обшивки (узел 2 — пом. 1, лист 54; узел 4 — пом. 2, 3, лист 55).
6. Примыкание к стенам: теневой шов 15 мм, техзазор 3 мм — пом. 1, 2, 3, 5, по стенам, выровненным штукатуркой (узел 1); пом. 4 — разделительная лента.
7. Светильники и потолочные устройства — подложка с планов освещения, слаботочных систем и вентиляции (положение — по ним); вырезы и закладные — по ведомости на листе, до обшивки; отверстия не совмещать с профилями, глубина корпуса светильника до 70 мм.
8. Разрезы 1–1, 2–2 — на листе 54; высоты мебели и дверных блоков сверены с низом потолка в разрезах; гибка бортов фигур и ленты ниш — там же; размеры фигурных уровней — фрагмент 1 (лист 55).
9. Узлы по выноскам на плане: узлы 1, 2, 3 — лист 54; узел 4 — лист 55; сечения М 1:10 по помещениям — лист 56.
10. Шпаклевание ГКЛ и условия приёмки — Q3: рассеянный дневной свет, осмотр с 2 м; боковой свет не оценивается.
11. Люки ревизии 300×300 мм — по центру блоков питания LED (БП4, БП1, БП2; координаты — план освещения).

1000 мм · печать 1:1

Изм.	Кол.уч	Лист	№ док.	Подп.	Дата
Разраб.		Кырлан А.С.			13.11.26
Пров.					
ГИП					
Н. контр.					
Утв.					

ГД-2026-011-АИ

Квартира 56 м²

ЖК «Северный парк», Москва

Дизайн-проект интерьера

Стадия	Лист	Листов
РП	53	119

План потолков

М 1:50

Кырлан Александр Сергеевич

выпуск 13.11.2026 № eb78108814f · стр. 59 из 139


Разрезы и узлы потолков

Разрезы по потолкам с отметками уровней · узлы коробов и ниш · размеры в мм

ПРЕДВАРИТЕЛЬНО · не для производства работ · открыто пунктов: 13 (реестр — л. 6, 7)


Разрез 1–1 (М 1:40)

Пом. 1 Гостиная-кухня; линия разреза — план потолков, лист 53

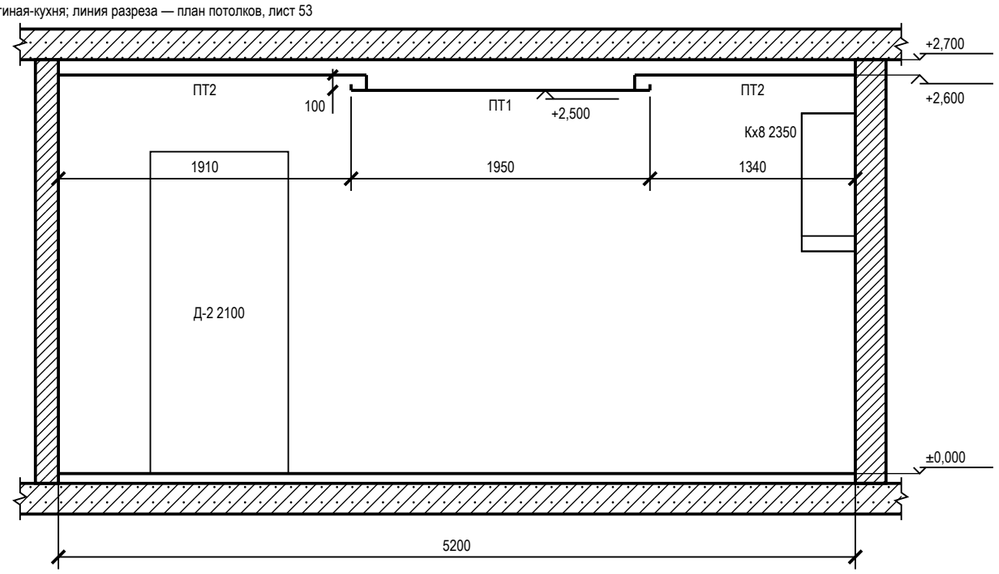


Разрез 2–2 (М 1:40)

Пом. 2 Спальня; линия разреза — план потолков, лист 53

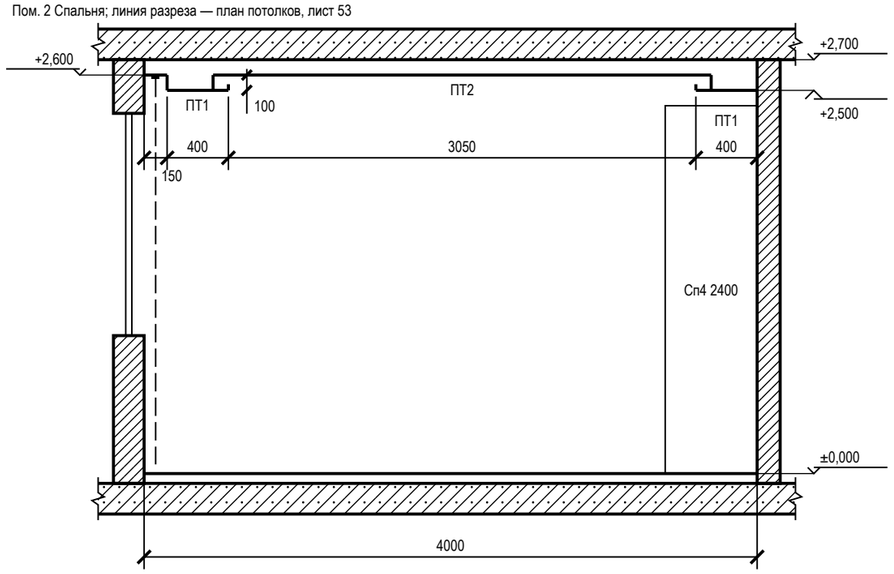

1 Короб с LED-подсветкой, теневой шов (М 1:10)


Пом. 2, 3; карниз 100×100, щель под свет 60 мм

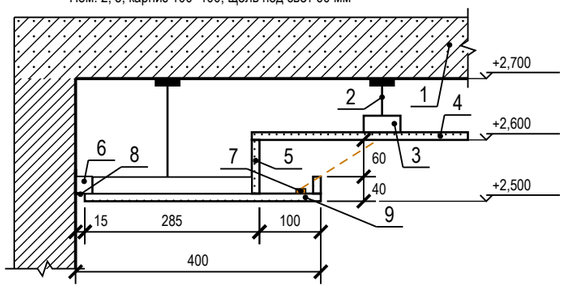

1 — плита перекрытия
2 — подвес прямой, шаг 1000 мм
3 — ПП 60×27: несущие через 500, основные через 1200 мм
4 — ГКЛ 12,5 по П113 — верхний уровень
5 — задняя стенка и бортик карниза — ГКЛ 12,5
6 — ПН 28×27 по периметру, к стене через 500 мм
7 — LED-лента в алюминиевом профиле
8 — теневой профиль: шов 15 мм, зазор 3 мм
9 — низ короба — ГКЛ 12,5 по ПП 60×27

2 Ниша под шторы (М 1:10)


Пом. 1; без подсветки; закладные под карниз — до обшивки

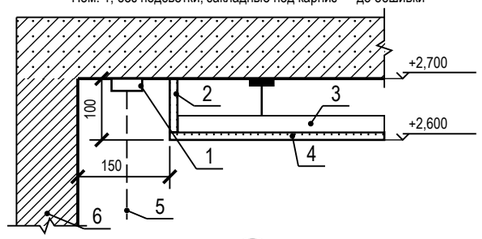

1 — карниз (шина), высота с верхом портьеры 80 мм
2 — стенка ниши — ГКЛ 12,5
3 — ПП 60×27 — каркас короба
4 — низ короба нижнего уровня — ГКЛ 12,5
5 — портьера
6 — стена с окном

3 Ниша LED фигурного уровня (М 1:10)

Пом. 1; карниз 100×100, щель под свет 60 мм

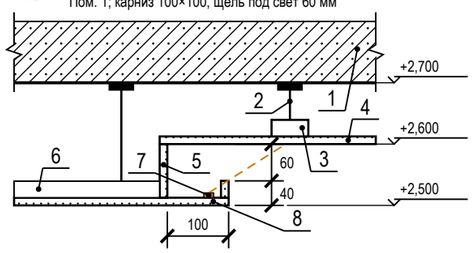

1 — плита перекрытия
2 — подвес прямой, шаг 1000 мм
3 — ПП 60×27: несущие через 500, основные через 1200 мм
4 — ГКЛ 12,5 по П113 — верхний уровень
5 — задняя стенка и бортик карниза — ГКЛ 12,5
6 — ПП 60×27 каркаса нижнего уровня, ПН по контуру фигуры (на дуге — с надрезами)
7 — LED-лента в алюминиевом профиле
8 — низ короба — ГКЛ 12,5 по ПП 60×27

Условные обозначения

- плита перекрытия в сечении
- стена в сечении
- потолок ГКЛ в сечении; под линией — марка потолка (план потолков)
- мебель и дверные проёмы за секущей плоскостью; число — марка и верх от чистого пола, мм
- портьера в нише под шторы

Допущения и предложения на листе. Основа листа: размеры помещений и положение проёмов введены заказчиком в брифе, не замерены (К-1); высота потолка 2700 мм — по брифу заказчика, не замерена (К-2); толщины стен приняты по брифу: наружные 200 мм, внутренние 150 мм — не обмерены (К-1); тип дома монолитный, перекрытие 200 мм — по брифу заказчика, документов нет (К-3); планировка (стены, проёмы, объединение кухни и гостиной, расширение санузла) — по брифу без обмера и плана БТИ (К-7); разрешённая мощность 10 кВт принята, ТУ не переданы (К-8); вентканалы приняты, в брифе не заданы (К-9); подрайон климата не задан — принят не северный (жилые от 2,5 м) (К-10). См. лист открытых вопросов (лист 6, записи К-1–К-3, К-7–К-10).

Примечания

1. Разрезы — по линиям 1–1, 2–2 на плане потолков (лист 53). Отметки — от ±0,000 чистого пола, м; размеры — мм.
2. Высоты мебели и дверных блоков за секущей плоскостью сверены с низом потолка над ними: верх ниже низа короба и поля.
3. ГКЛ 12,5 мм по каркасу П113; перепад уровней и бортик карниза — ГКЛ по ПП 60×27 (узел 1 — на этом листе). Ниша под шторы — на всю длину стены с окном, карниз на закладной до обшивки (узел 2 — на этом листе; узел 4 — лист 55).
4. Толщины плит перекрытия и пирога пола показаны условно.
5. Сечения потолков по помещениям М 1:10 (отметки помещения, профили, подвесы, крепёж, изделия) — лист 56.
6. Ведомость объёмов потолков (лист ГКЛ, профиль, подвесы, лента, блоки питания, люки) — на листе 55.
7. Фрагмент 1 — помещение с фигурными уровнями (размеры фигур, радиусы, отметки) — на листе 55.

1000 мм · печать 1:1

Изм.	Кол.уч	Лист	№ док.	Подп.	Дата
Разраб.		Кырлан А.С.			13.11.26
Пров.					
ГИП					
Н. контр.					
Утв.					

ГД-2026-011-АИ

Квартира 56 м²

ЖК «Северный парк», Москва

Дизайн-проект интерьера

Стадия	Лист	Листов
РП	54	119

Разрезы и узлы потолков

М 1:40; 1:10

Кырлан Александр Сергеевич


выпуск 13.11.2026 № eb7810814f · стр. 60 из 139

Разрезы и узлы потолков (продолжение)

Узлы коробов и ниш · фрагменты фигурных уровней · ведомость объёмов · размеры в мм

Фрагмент 1. Пом. 1 Гостиная-кухня — уровни потолка (М 1:50)

Цепочки — от чистых граней стен; отметки — низ уровня от ±0,000

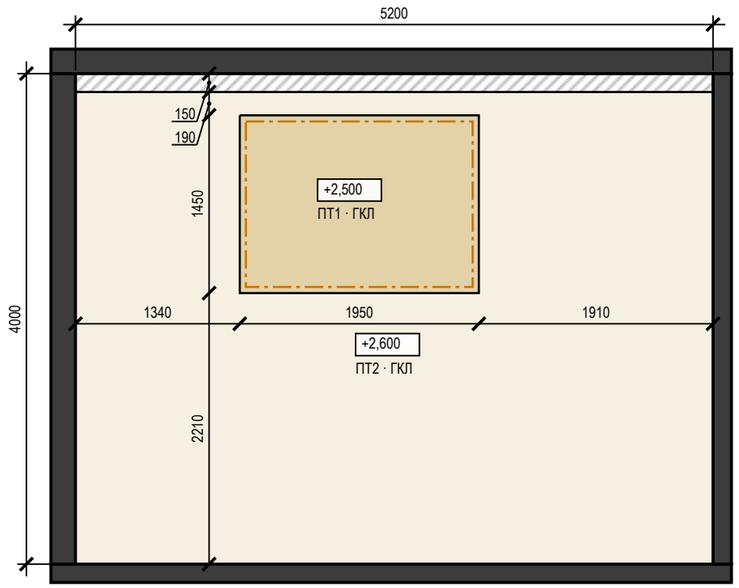

ПТ1 — низ +2,500

ПТ2 — низ +2,600

LED-лента в нише подсветки (карниз короба, ниша фигуры)


ниша под шторы

Ведомость объёмов потолков

Позиция	Ед.	Кол.	Пом.
Лист ГКЛ 12,5	м²	59,20	1, 2, 3, 5
Лист ГКЛВ 12,5	м²	4,81	4
Борта и карнизы (входят в площади листов выше)	м²	7,64	1, 2, 3
Профиль ПП 60×27	м	169,21	1, 2, 3, 4, 5
Профиль ПН 28×27	м	169,50	1, 2, 3, 4, 5
Подвес прямой	шт.	72	1, 2, 3, 4, 5
Анкер-клин к плите	шт.	72	1, 2, 3, 4, 5
Шуруп TN 3,5×25	шт.	1472	1, 2, 3, 4, 5
Лента армирующая для швов	м	76,81	1, 2, 3, 4, 5
Шпаклёвка для швов	кг	25,60	1, 2, 3, 4, 5
Грунтовка (швы)	л	6,40	1, 2, 3, 4, 5
Лента разделительная по периметру	м	65,70	1, 2, 3, 4, 5
Сплошная шпаклёвка и окраска (площадь развёртки)	м²	64,01	1, 2, 3, 4, 5
Лента LED	м	26,80	1, 2, 3
Требуемая мощность блоков питания	Вт	334	1, 2, 3
Установленная мощность блоков питания	Вт	700	1, 2, 3
Блок питания LED	шт.	3	1, 2, 3
Люк ревизии	шт.	3	1, 2, 3

4 Ниша под шторы (М 1:10)

Пом. 2, 3; без подсветки; закладные под карниз — до обшивки

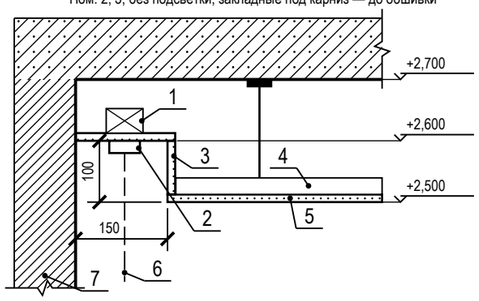

1 — закладная под карниз — брус 40×50
2 — карниз (шина), высота с верхом портьеры 80 мм
3 — стенка и потолок ниши — ГКЛ 12,5
4 — ПП 60×27 — каркас короба
5 — низ короба нижнего уровня — ГКЛ 12,5
6 — портьера
7 — стена с окном

Допущения и предложения на листе

Основа листа: размеры помещений и положение проёмов введены заказчиком в брифе, на объекте не замерены (К-1); высота потолка 2700 мм — по брифу заказчика, не замерена (К-2); толщины стен приняты по брифу: наружные 200 мм, внутренние 150 мм — не обмерены (К-1); тип дома монолитный, перекрытие 200 мм — по брифу заказчика, документов нет (К-3); планировка (стены, проёмы, объединение кухни и гостиной, расширение санузла) — по брифу без обмера и плана БТИ (К-7); разрешённая мощность 10 кВт принята, ТУ не переданы (К-8); вентканалы приняты, в брифе не заданы (К-9); подрайон климата не задан — принят не северный (жилые от 2,5 м) (К-10).
См. лист открытых вопросов (лист 6, записи К-1–К-3, К-7–К-10).

Примечания

1. ГКЛ 12,5 мм по каркасу П113; узлы коробов и ниш под шторы: узел 1 — лист 54; узел 2 — лист 54; узел 4 — на этом листе; условные обозначения разрезов — на листе 54.
2. Фрагмент 1 (план потолков — лист 53) — фигурные уровни потолка крупно: привязки краёв и центров фигур к чистым граням стен, радиусы (R) с центрами, хорда и стрелка дуги, отметки низа каждого уровня; цвета уровней — как на плане потолков.
3. Фигурные уровни: борт — ГКЛ по ПН с надрезами (на дуге шаг стоек борта 300 мм при R до 2500, 400 — до 5000) или по гнутому заводскому профилю (СП 163, 6.3.3). Лента в нише фигуры по оси: остров пом. 1 — 6,4 м; узел ниши LED фигуры: узел 3 — лист 54 — пом. 1.
4. Ведомость объёмов — по геометрии плана потолков: Лист ГКЛ 12,5 — плоскости уровней + борта (без арочных участков); Лист ГКЛВ 12,5 — плоскости уровней + борта; Борта и карнизы — длина перепада × перепад; Профиль ПП 60×27 — S × (1/шаг несущ. + 1/шаг осн.) + стойки бортов; Профиль ПН 28×27 — периметр стен + 2 × перепады + карнизы; Подвес прямой — по раскладке: S уровня / (шаг осн. × шаг подвесов), пояс уже шага — ряд вдоль пояса, фигура — по контуру; шаг подвесов — не больше табл. 14 СП 163; Анкер-клин к плите — по одному на подвес (Knauf П113); Шуруп TN 3,5×25 — 23 шт./м² (Knauf П113, табл. 2 альбома П 11); Лента армирующая для швов — 1,2 м/м² листа (Knauf); Шпаклёвка для швов — 0,4 кг/м² листа, только швы (Knauf); Грунтовка (швы) — 0,1 л/м² листа, только швы (Knauf); Лента разделительная по периметру — периметр стен под потолком ГКЛ; Сплошная шпаклёвка и окраска (площадь развёртки) — плоскости + борта; расход — по паспорту материала (норма расхода на сплошной слой не подтверждена); Лента LED — по оси карниза и ниши фигуры (план потолков); Требуемая мощность блоков питания — Вт/м × длина × 1,3; Установленная мощность блоков питания — сумма мощностей блоков по плану освещения; Блок питания LED — блоки потолочных лент по плану освещения (БП4, БП1, БП2); Люк ревизии — план потолков; без запаса на подрезку (при закупке листа: ×1,075 при S > 20 м², ×1,175 — 10–20 м², ×1,275 — < 10 м²).

1000 мм · печать 1:1

Изм.	Кол.уч	Лист	№ док.	Подп.	Дата			
Разраб.		Кырлан А.С.			13.11.26	ГД-2026-011-АИ		
Пров.						Квартира 56 м²		
ГИП						ЖК «Северный парк», Москва		
						Дизайн-проект интерьера	Стадия: РП	Лист: 55 / Листов: 119
Н. контр.						Разрезы и узлы потолков (продолжение)	Кырлан Александр Сергеевич	
Утв.						М 1:50; 1:10		


выпуск 13.11.2026 № eb7810814f · стр. 61 из 139

Сечения потолков М 1:10

Пом. 1, 2, 3 · профили, подвесы, крепёж, изделия · размеры в мм

Сечение 1.1. Ниша LED фигурного уровня (М 1:10)


Пом. 1 Гостиная-кухня; карниз 100×100, щель под свет 60 мм

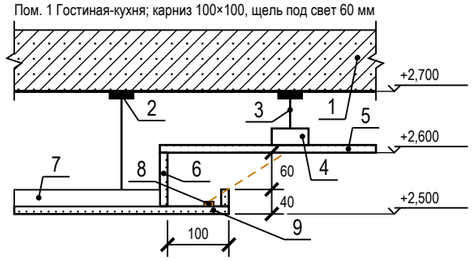

1 — плита перекрытия
2 — анкер-клин к плите — по одному на подвес
3 — подвес прямой, шаг 1000 мм
4 — ПП 60×27: несущие через 500, основные через 1200 мм; соединители одноуровневые, шурупы LN 3,5×9
5 — ГКЛ 12,5 по П113 — верхний уровень; шурупы TN 3,5×25 через 170 мм
6 — задняя стенка и бортик карниза — ГКЛ 12,5
7 — ПП 60×27 каркаса нижнего уровня, ПН по контуру фигуры (на дуге — с надрезами)
8 — LED-лента 9,6 Вт/м, 24 В в алюминиевом профиле
9 — низ короба — ГКЛ 12,5 по ПП 60×27

Сечение 1.2. Ниша под шторы (М 1:10)


Пом. 1 Гостиная-кухня; без подсветки; закладные под карниз — до обшивки

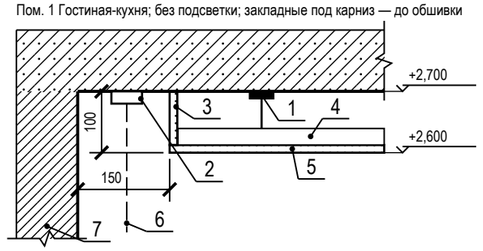

1 — анкер-клин к плите — по одному на подвес; подвес прямой, шаг 1000 мм
2 — карниз (шина), высота с верхом портьеры 80 мм
3 — стенка ниши — ГКЛ 12,5
4 — ПП 60×27 — каркас короба, основные через 1200 мм; соединители одноуровневые, шурупы LN 3,5×9
5 — низ короба нижнего уровня — ГКЛ 12,5; шурупы TN 3,5×25 через 170 мм
6 — портьера
7 — стена с окном

Сечение 1.3. Примыкание потолка к стене (М 1:10)


Пом. 1 Гостиная-кухня; примыкание — теневой шов

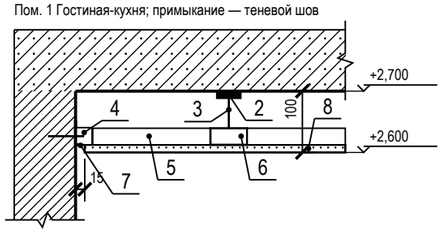

1 — плита перекрытия
2 — анкер-клин к плите — по одному на подвес
3 — подвес прямой, шаг 1000 мм
4 — ПН 28×27 по периметру — дюбель-гвоздь через ≤ 500 мм, не менее 3 на профиль
5 — ПП 60×27 несущий (вид) через 500 мм, в ПН
6 — ПП 60×27 основной (сечение) через 1200 мм; соединители одноуровневые, шурупы LN 3,5×9
7 — теневой профиль: шов 15 мм, зазор 3 мм; стена под шов выровнена
8 — ГКЛ 12,5 по П113; шурупы TN 3,5×25 через 170 мм

Сечение 2.1. Короб с LED-подсветкой, теневой шов (М 1:10)


Пом. 2 Спальня, 3 Детская; карниз 100×100, щель под свет 60 мм

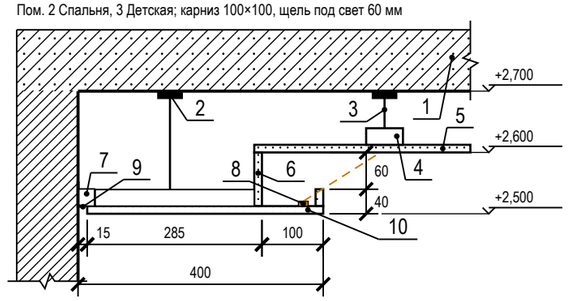

1 — плита перекрытия
2 — анкер-клин к плите — по одному на подвес
3 — подвес прямой, шаг 1000 мм
4 — ПП 60×27: несущие через 500, основные через 1200 мм; соединители одноуровневые, шурупы LN 3,5×9
5 — ГКЛ 12,5 по П113 — верхний уровень; шурупы TN 3,5×25 через 170 мм
6 — задняя стенка и бортик карниза — ГКЛ 12,5
7 — ПН 28×27 по периметру — дюбель-гвоздь через ≤ 500 мм, не менее 3 на профиль
8 — LED-лента 9,6 Вт/м, 24 В в алюминиевом профиле
9 — теневой профиль: шов 15 мм, зазор 3 мм
10 — низ короба — ГКЛ 12,5 по ПП 60×27

Сечение 2.2. Ниша под шторы (М 1:10)

Пом. 2 Спальня, 3 Детская; без подсветки; закладные под карниз — до обшивки

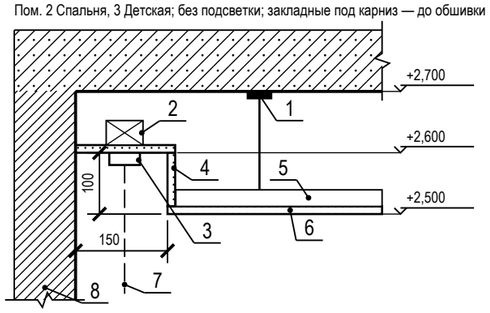

1 — анкер-клин к плите — по одному на подвес; подвес прямой, шаг 1000 мм
2 — закладная под карниз — брус 40×50
3 — карниз (шина), высота с верхом портьеры 80 мм
4 — стенка и потолок ниши — ГКЛ 12,5
5 — ПП 60×27 — каркас короба, основные через 1200 мм; соединители одноуровневые, шурупы LN 3,5×9
6 — низ короба нижнего уровня — ГКЛ 12,5; шурупы TN 3,5×25 через 170 мм
7 — портьера
8 — стена с окном

Условные обозначения

— · — LED-лента в нише подсветки (карниз короба, ниша фигуры)

Допущения и предложения на листе

Основа листа: размеры помещений и положение проёмов введены заказчиком в брифе, на объекте не замерены (К-1); высота потолка 2700 мм — по брифу заказчика, не замерена (К-2); толщины стен приняты по брифу: наружные 200 мм, внутренние 150 мм — не обмерены (К-1); тип дома монолитный, перекрытие 200 мм — по брифу заказчика, документов нет (К-3); планировка (стены, проёмы, объединение кухни и гостиной, расширение санузла) — по брифу без обмера и плана БТИ (К-7); разрешённая мощность 10 кВт принята, ТУ не переданы (К-8); вентканалы приняты, в брифе не заданы (К-9); подрайон климата не задан — принят не северный (жилые от 2,5 м) (К-10).
См. лист открытых вопросов (лист 6, записи К-1–К-3, К-7–К-10).

Примечания

1. Сечения потолков М 1:10 по помещениям с нишами LED и нишами под шторы: отметки и размеры этого помещения от ±0,000 чистого пола (м, мм). Положение — по плану потолков (лист 53): короб и ниша LED — по линиям ленты, ниша под шторы — у стены с окном; типовые узлы по группам помещений — на листе 54.
2. Крепёж: подвес прямой к плите на анкер-клине — по одному на подвес (Knauf П113); ПН к стенам — дюбель-гвоздь через ≤ 500 мм, не менее 3 на профиль (серия 1.045.9-2.08); лист 12,5 — шурупы TN 3,5×25 через 170 мм (СП 163, табл. 15); профили между собой — соединители одноуровневые, шурупы LN 3,5×9.
3. Изделие карниза, профиля LED и галтели подписано артикулом из данных; где артикул не выбран, сечение дано по габаритам из данных (ширина и глубина ниши, щель под свет), изделие подбирается по ним.

1000 мм · печать 1:1

Изм.	Кол.уч	Лист	№ док.	Подп.	Дата
Разраб.		Кырлан А.С.			13.11.26
Пров.					
ГИП					
Н. контр.					
Утв.					

ГД-2026-011-АИ

Квартира 56 м²

ЖК «Северный парк», Москва

Дизайн-проект интерьера

Стадия	Лист	Листов
РП	56	119

Сечения потолков М 1:10

М 1:10

Кырлан Александр Сергеевич


выпуск 13.11.2026 № eb7810814f · стр. 62 из 139

Раскладка плитки. Планы полов

Раскладка от чистовых размеров · размеры в мм · отметки от ±0,000

ПРЕДВАРИТЕЛЬНО · не для производства работ · открыто пунктов: 13 (реестр — л. 6, 7)

Фрагмент 1. Санузел (пом. 4). Пол 600×600, шов 2 мм (М 1:20)

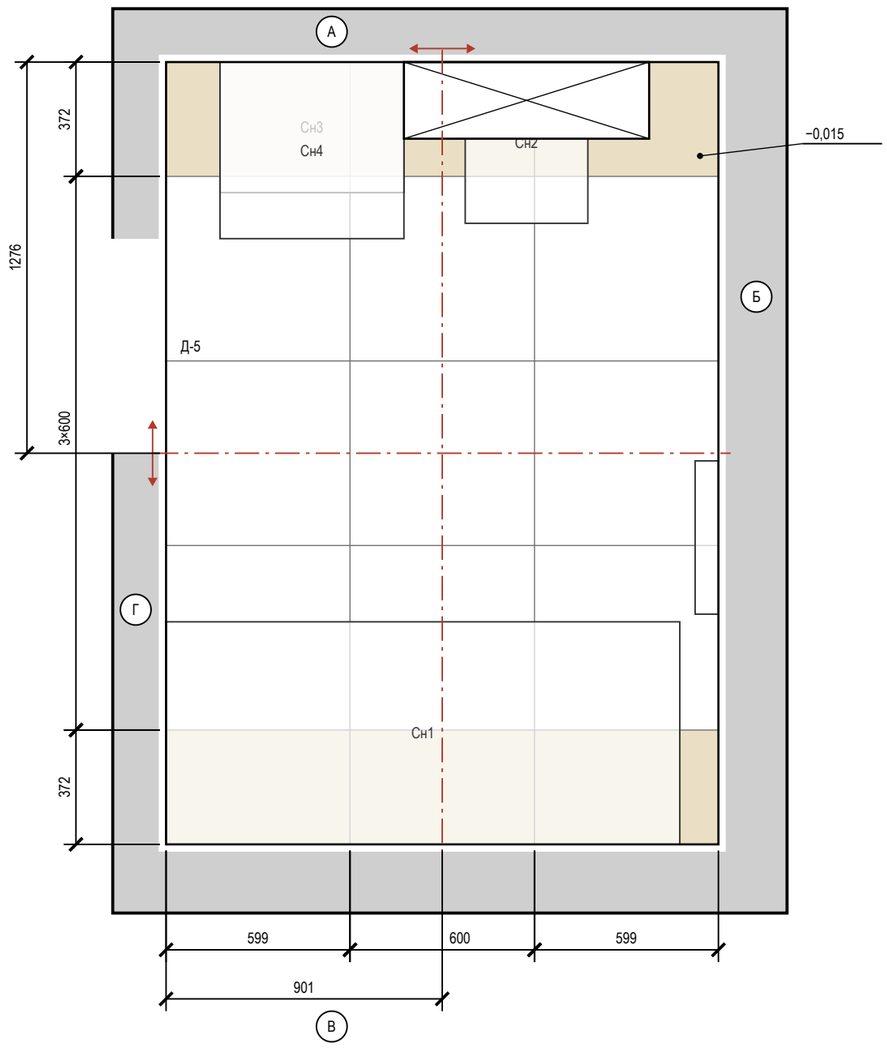

Ведомость плитки

Помещение, поверхность	Плитка, код	Формат	Шов	S, м²	Целых	Подр.	С запасом
Санузел, пол	аналог: керамогранит под травертин	600×600	2	4,81	9	6	17
Санузел, стены А–Г	A8UZ	600×1200	2	18,97	18	14	36
Санузел, короб инсталляции	A8UZ	600×1200	2	1,76	0	6	7
Прихожая, пол	A8UZ	600×1200	2	8,58	4	14	20
Гостиная-кухня, фартук (ст. Г)	аналог: керамогранит под травертин, матовый	1200×600	2	1,82	0	5	6
Итого 600×600				4,81	9	6	17
Итого 600×1200				**31,13**	**22**	**39**	**69**

Условные обозначения

- плитка целая; тонкая линия — шов
- плитка с подрезкой (размер — на цепочке)
- ось старта; стрелки — направление укладки
- сантехприбор: габарит, высота по практике
- короб инсталляции: плитка пола — до короба
- отметка чистого пола на полке выноски, м
- (А) обозначение стены А–Г (как на развёртках)

Ведомость материалов

Материал	Класс, код	Норма расхода	Кол-во
Затирка	CG2WA Mapei Ultracolor Plus 132	(a+b)/ab·шов·t·1,6	2,1 кг
Затирка	CG2WA	(a+b)/ab·шов·t·1,6	0,8 кг
Клей	C2 TE S1 Ceresit CM 17	1,2 кг/м²·мм, слой 5	163 кг (7 меш.)
Клей	C2 TE S1	1,2 кг/м²·мм, слой 5	68 кг (3 меш.)
Гидроизоляция	обмазочная, 2 слоя: пол, стены по периметру и зоны замачивания	по ТУ	12,4 м²
Демпф. лента	по периметру пола из плитки		16,9 м

Примечания

1. Раскладка от чистовых размеров: стены санузлов теряют 10 + 5 + 9 = 24 мм на сторону (штукатурка, клей, плитка); подрезки — чистые, без шва.
2. Старт — от центра помещения (штрихпунктир, стрелки — направление укладки); размер старта — от чистовых стен Г и А.
3. Раскладка пола «Прихожая» и фартука «Гостиная-кухня» — на листе «Раскладка плитки. Прихожая. Фартук кухни».
4. Калибр партии не задан — до укладки замерить (рабочий размер W, ГОСТ 13996-2019) и пересчитать подрезки.
5. Количество: целые по раскладке + по одной на подрезку, запас 10 %; один артикул — одна партия и тон. Исключены поддон, короб, проёмы и места за коробом; S — по чистым граням: стены нетто = зона облицовки по ведомости отделки − место за коробом инсталляции 0,96 м² (плитку за коробом не кладут), короб — отдельной строкой.
6. Клей C2 TE S1 Ceresit CM 17; C2 TE S1 (ГОСТ Р 56387-2018), затирка CG2WA Mapei Ultracolor Plus 132; CG2WA; расход — по ТУ выбранной марки.
7. Гидроизоляция: пол и стены 200 мм от ЧП; над ванной — до 2000 и 300 мм за борт (см. развёртки); акт скрытых работ, пролив 24 ч.
8. Швы пола совмещены со швами стены А; по периметру — демпферная лента.
9. Отметка чистого пола −0,015, порог 15 мм; стык с соседним покрытием — по оси полотна двери.

Допущения и предложения на листе

Основа листа: размеры помещений и положение проёмов введены заказчиком в брифе, на объекте не замерены (К-1); высота потолка 2700 мм — по брифу заказчика, не замерена (К-2); толщины стен приняты по брифу: наружные 200 мм, внутренние 150 мм — не обмерены (К-1); тип дома монолитный, перекрытие 200 мм — по брифу заказчика, документов нет (К-3); планировка (стены, проёмы, объединение кухни и гостиной, расширение санузла) — по брифу без обмера и плана БТИ (К-7); разрешённая мощность 10 кВт принята, ТУ не переданы (К-8); вентканалы приняты, в брифе не заданы (К-9); подрайон климата не задан — принят не северный (жилые от 2,5 м) (К-10).

Знак «**» — предложение проектировщика, заказчиком не утверждено (согласовать с заказчиком): пол пом. 4 — пирог пола: стяжка 33 мм и обмазочная гидроизоляция добавлены разработчиком проекта; артикул изделия не выбран: позиция описана характеристиками («аналог по характеристикам»), артикул выбирается при закупке.

См. лист открытых вопросов (лист 6, записи К-1–К-3, К-7–К-10).

1000 мм · печать 1:1

Изм.	Кол.уч	Лист	№ док.	Подп.	Дата
Разраб.		Кырлан А.С.			13.11.26
Пров.					
ГИП					
Н. контр.					
Утв.					

ГД-2026-011-АИ

Квартира 56 м²

ЖК «Северный парк», Москва

Дизайн-проект интерьера

Стадия	Лист	Листов
РП	57	119

Раскладка плитки. Планы полов

М 1:20

Кырлан Александр Сергеевич


выпуск 13.11.2026 № eb78108141 · стр. 63 из 139

Раскладка плитки. Прихожая. Фартук кухни


Раскладка от чистовых размеров · размеры в мм · высоты фартука от чистого пола

ПРЕДВАРИТЕЛЬНО · не для производства работ · открыто пунктов: 13 (реестр — л. 6, 7)

Фрагмент 1. Прихожая (пом. 5). Пол 600×1200, шов 2 мм (М 1:25)

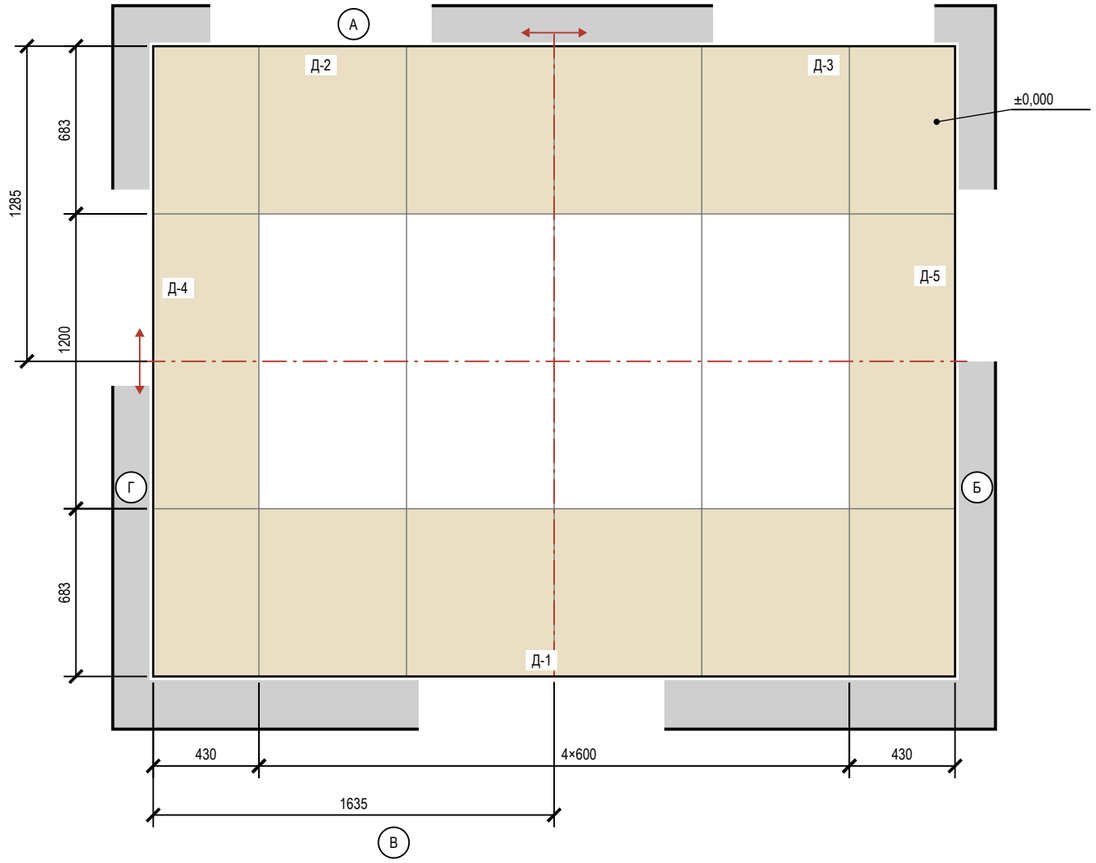

Фрагмент 2. Гостиная-кухня (пом. 1), фартук, стена Г. 1200×600, шов 2 мм (М 1:25)

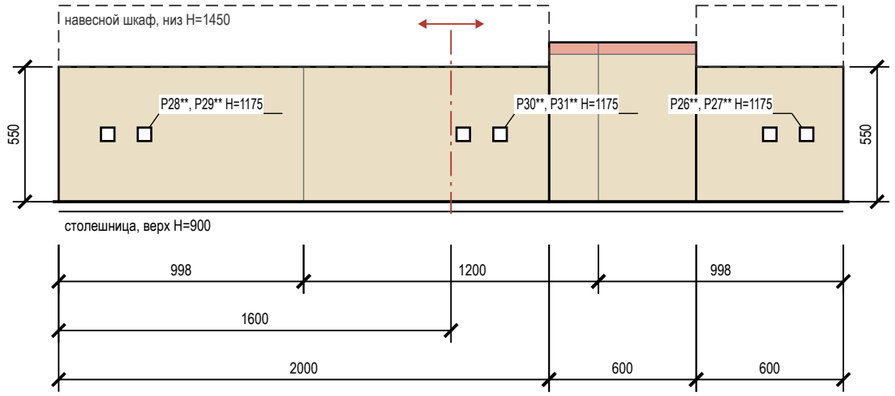

Условные обозначения

- плитка целая; тонкая линия — шов
- плитка с подрезкой (размер — на цепочке)
- ось старта; стрелки — направление укладки
- электроточка: марка и Н — по листам ЭОМ
- столешница (верх)
- навесной шкаф над фартуком
- отметка чистого пола на полке выноски, м
- (А) обозначение стены А–Г (как на развёртках)

Подсчёт плитки

Поверхность	Формат	S, м²	Целых	Подр.	С запасом
Прихожая, пол	600×1200	8,58	4	14	20
Гостиная-кухня, фартук (ст. Г)	1200×600	1,82	0	5	6

Примечания

1. Прихожая: керамогранит 600×1200, длинная сторона — вдоль стен Б и Г, шов 2 мм, прямая раскладка от центра. Стены окрашены: раскладка от чистового контура минус штукатурка и шпаклёвка 15 мм на сторону (принято); подрезки 430 / 683 мм, срез — под плинтус.
2. Прихожая: деформационный зазор по периметру 8–10 мм под плинтусом; в проёмах — стык с соседним покрытием по оси полотна двери. Клей C2 TE S1, затирка CG2WA.
3. Фартук, Гостиная-кухня: 1200×600 горизонтально, шов 2 мм; зоны 600 мм — 900…1450, 600 мм — 900…1550, 2000 мм — 900…1450 (от столешницы до низа навесного шкафа, без шкафа — 650 мм). Старт от центра участка, подрезки 998 мм. Площадь 1,82 м² — как в ведомости отделки.
4. Фартук — после монтажа столешницы, низ на 2–3 мм выше неё, шов со столешницей — санитарный герметик; навесные шкафы — после фартука. Торцы у пенала и стены — профиль или запил 45°.
5. Фартук, Гостиная-кухня: в зоне до отм. 1550 верхний ряд подрезан 48 мм — меньше 1/3 плитки; полоса прикрыта корпусом навесного модуля и на виду не остаётся. Раскладкой не снимается: убрать подрезку можно, только выровняв низ этого модуля с соседними (1450 мм) — решение мебельщика.
6. Клей, затирка и итог по форматам — в ведомостях листа «Раскладка плитки. Планы полов».

Допущения и предложения на листе

Основа листа: размеры помещений и положение проёмов введены заказчиком в брифе, на объекте не замерены (К-1); высота потолка 2700 мм — по брифу заказчика, не замерена (К-2); толщины стен приняты по брифу: наружные 200 мм, внутренние 150 мм — не обмерены (К-1); тип дома монолитный, перекрытие 200 мм — по брифу заказчика, документов нет (К-3); планировка (стены, проёмы, объединение кухни и гостиной, расширение санузла) — по брифу без обмера и плана БТИ (К-7); разрешённая мощность 10 кВт принята, ТУ не переданы (К-8); вентканалы приняты, в брифе не заданы (К-9); подрайон климата не задан — принят не северный (жилые от 2,5 м) (К-10).

Знак «**» — предложение проектировщика, заказчиком не утверждено (согласовать с заказчиком): P26, P27, P28, P29, P30, P31 — Сдвиг под раскладку плитки фартука (стена Г) на 75 мм выше — ось на шве или в центре плитки, привязка по таблице листа; плинтус пом. 1, 5, фартук пом. 1 — артикул изделия не выбран: позиция описана характеристиками («аналог по характеристикам»), артикул выбирается при закупке.

См. лист открытых вопросов (лист 6, записи К-1–К-3, К-7–К-10).

1000 мм · печать 1:1

Изм.	Кол.уч	Лист	№ док.	Подп.	Дата
Разраб.		Кырлан А.С.			13.11.26
Пров.					
ГИП					
Н. контр.					
Утв.					

ГД-2026-011-АИ

Квартира 56 м²

ЖК «Северный парк», Москва

Дизайн-проект интерьера

Стадия	Лист	Листов
РП	58	119

Раскладка плитки. Прихожая. Фартук кухни


М 1:25

Кырлан Александр Сергеевич

Раскладка плитки. Санузел. Развёртки стен

ПРЕДВАРИТЕЛЬНО · не для производства работ · открыто пунктов: 13 (реестр — л. 6, 7)

Пом. 4 · вид изнутри помещения · размеры в мм · высоты от чистого пола, отметки от ±0,000

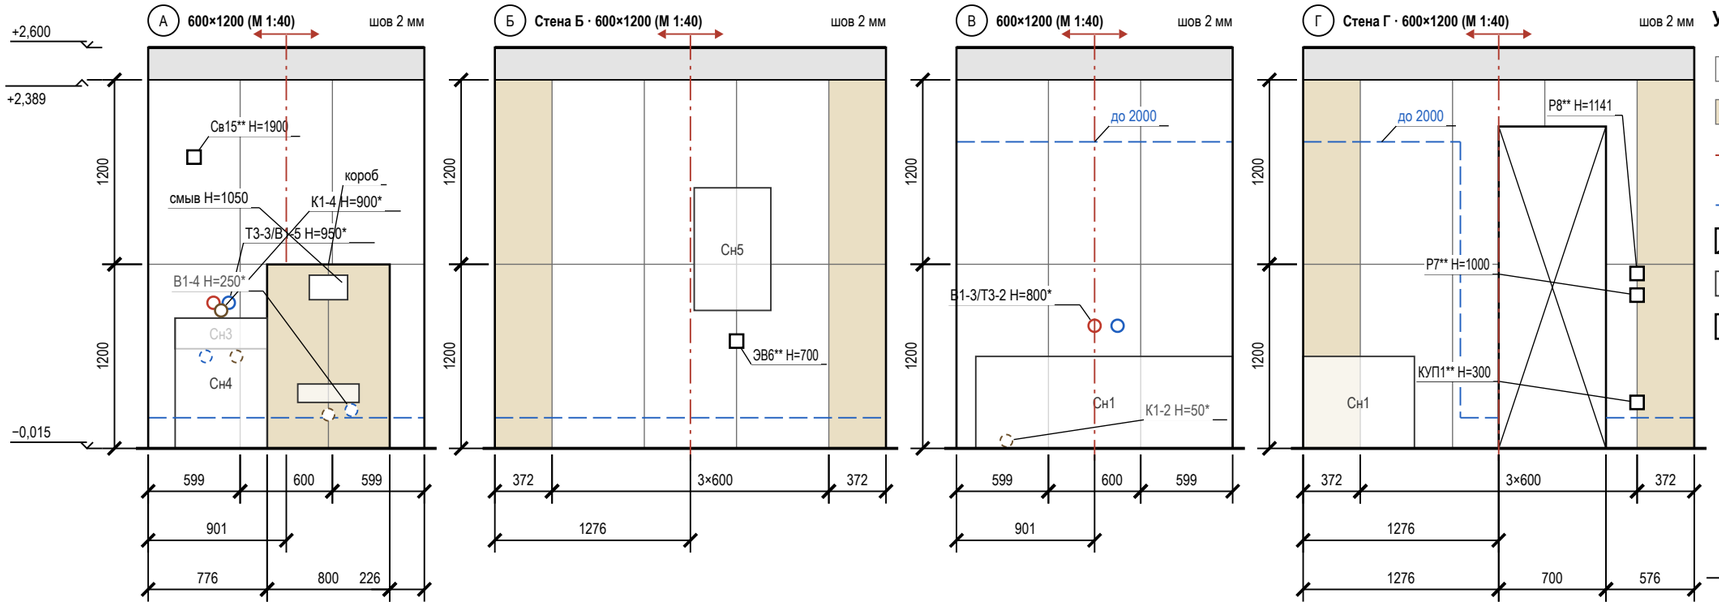

Условные обозначения

- плитка целая; тонкая линия — шов
- плитка с подрезкой (размер — на цепочке)
- ось старта; стрелки — направление укладки
- верх гидроизоляции: 200 от ЧП, в мокрой зоне — «до …»
- проём — не облицовывается
- сантехприбор: габарит, высота по практике
- короб инсталляции, в нём кнопка смыва 250×160
- вывод В1 (код — в ведомости привязок)
- вывод Т3 (код — в ведомости привязок)
- вывод К1 (код — в ведомости привязок)
- вывод за прибором / в коробе (не на сетке)
- электроточка: марка и Н — по листам ЭОМ
- отметка уровня, м: ±0,000 — чистый пол жилых помещений
- низ потолка; серая полоса — стена без плитки
- А обозначение стены А–Г (как на развёртках)

Подсчёт плитки по стенам и коробу

Поверхность	L × H, мм	S, м²	Целых	Подр.	С запасом	Подрезки: край / верх, мм
стена А	1802 × 2404	3,49	4	2	7	599 / 599; целый ряд
короб (ст. А)	800×1200×250	1,76	0	6	7	лицо 399 / 399; бок. 250
стена Б	2552 × 2404	6,25	6	4	11	372 / 372; целый ряд
стена В	1802 × 2404	4,45	6	0	7	599 / 599; целый ряд
стена Г	2552 × 2404	4,78	2	8	11	372 / 372; целый ряд
Итого		**20,73**	**18**	**20**	**43**	

Примечания

1. Вид изнутри, стены по часовой стрелке А → Г. Высоты — от чистого пола (−0,015), отметки — от ±0,000. Раскладка от чистовых размеров (штукатурка 10 + клей 5 + плитка 9 мм), подрезки чистые; старт — от оси стены, ряды от пола целыми.
2. Облицовка не до потолка: верх плитки +2,389, выше — отделка стены по ведомости отделки до потолка +2,600; торец облицовки — профиль-окантовка.
3. Открытые выводы и электроточки — на шве или в центре плитки (допуск 10 мм; плитка от 900 мм по высоте — на шве или не ближе 60 мм к нему).
4. Выводы ВК стоят по оси прибора и с прибором не двигаются — привязки по «Плану выводов сантехники» без сдвига; вне сетки (Т3-3/В1-5, К1-4, В1-3/Т3-2) — отверстие в плитке коронкой по той же привязке, плитку не сдвигать.
5. Выводы — по «Плану выводов сантехники», электроточки — по ЭОМ, «*» — высота по практике; за приборами и в коробе (В1-4, К1-3, В1-6, К1-5, К1-2) — штриховым кольцом.
6. Гидроизоляция: 200 мм от ЧП по периметру; над ванной — до 2000 и 300 мм за борт (СП 29.13330.2011, п. 7.2 — на высоту замачивания); углы — лентой; акт скрытых работ, пролив.
7. Короб 800×1200×250: лицо 399 / 399 мм от оси кнопки смыва, боковины, полка; углы — запил 45° или профиль; за коробом плитку не кладут.

Допущения и предложения на листе. Основа листа: размеры помещений и положение проёмов введены заказчиком в брифе, не замерены (К-1); высота потолка 2700 мм — по брифу заказчика, не замерена (К-2); толщины стен приняты по брифу: наружные 200 мм, внутренние 150 мм — не обмерены (К-1); тип дома монолитный, перекрытие 200 мм — по брифу заказчика, документов нет (К-3); планировка (стены, проёмы, объединение кухни и гостиной, расширение санузла) — по брифу без обмера и плана БТИ (К-7); разрешённая мощность 10 кВт принята, ТУ не переданы (К-8); вентканалы приняты, в брифе не заданы (К-9); подрайон климата не задан — принят не северный (жилые от 2,5 м) (К-10). Знак «**» — предложено, не утверждено (согласовать): пол пом. 4, Р7, Р8, Св15, КУП1, ЭВ6; К-5: дверь пом. 4 (стена Г). См. лист открытых вопросов (лист 6, записи К-1–К-3, К-5, К-7–К-10).

1000 мм · печать 1:1

Изм.	Кол.уч	Лист	№ док.	Подп.	Дата
Разраб.		Кырлан А.С.			13.11.26
Пров.					
ГИП					
Н. контр.					
Утв.					

ГД-2026-011-АИ

Квартира 56 м²

ЖК «Северный парк», Москва

Дизайн-проект интерьера

Стадия	Лист	Листов
РП	59	119

Раскладка плитки. Санузел. Развёртки стен

М 1:40

Кырлан Александр Сергеевич

07

Полы и отделка

Кырлан Александр Сергеевич

выпуск 13.11.2026 · eb7810814f · стр. 66 из 139

План полов


Покрытия, направление укладки, отметки чистого пола, стыки · размеры в мм · отметки в м

Условные обозначения

- тип 1 — инженерная доска, линии — вдоль доски
- тип 2 — керамогранит 600×600, сетка — формат плитки
- тип 3 — керамогранит 600×1200, сетка — формат плитки
- 1 — номер типа пола (экспликация полов)
- схема пола, без масштаба: плита — штриховка, стяжка — точки, звукоизоляция — зигзаг, гидроизоляция — утолщённая линия с заведением на стену
- направление укладки (длинная сторона доски)
- отметка чистого пола, м
- стык в проёме: Т-профиль по оси полотна
- стык в проёме: порог
- СТ1 — марка стыка (ведомость стыков)
- стояк: К1 — канализация, В1 ХВС, Т3 — ГВС
- новое — возводится по проекту (синим)
- 1 — номер помещения, площадь м²

Отметки по высоте

±0,000	чистый пол пом. 1–3, 5; отсчёт высот
−0,015	чистый пол пом. 4, ниже на 15 мм
−0,064*	верх плиты — расчёт, не замер (задание на обмер)
сущ. пол	снимается до плиты; не замерен (задание на обмер)

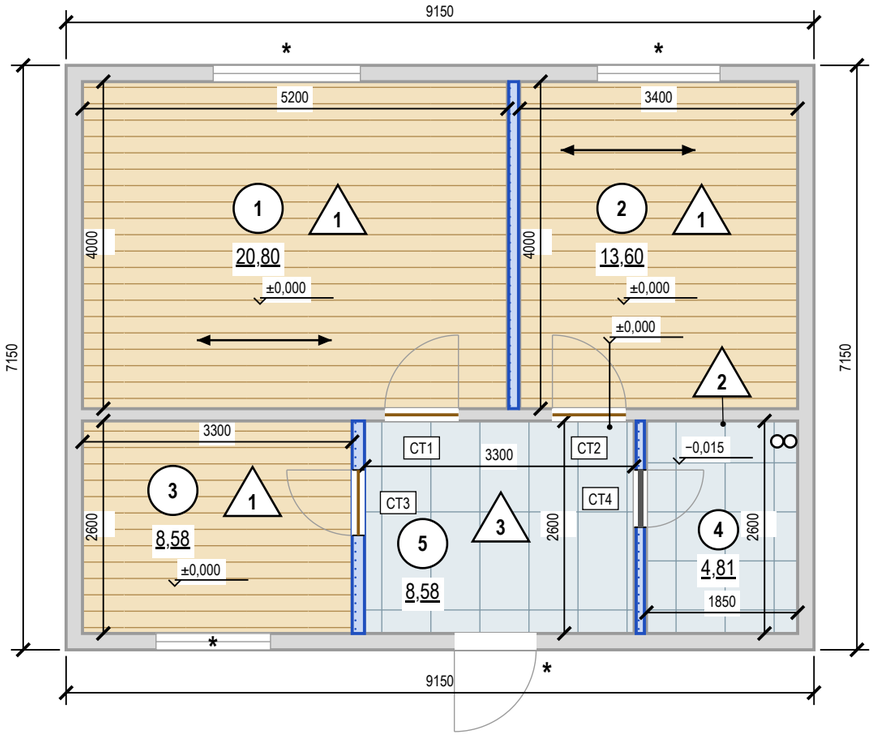

Допущения и предложения на листе. Основа листа: размеры помещений и положение проёмов введены заказчиком в брифе, на объекте не замерены (К-1); высота потолка 2700 мм — по брифу заказчика, не замерена (К-2); толщины стен приняты по брифу: наружные 200 мм, внутренние 150 мм — не обмерены (К-1); тип дома монолитный, перекрытие 200 мм — по брифу заказчика, документов нет (К-3); планировка (стены, проёмы, объединение кухни и гостиной, расширение санузла) — по брифу без обмера и плана БТИ (К-7); разрешённая мощность 10 кВт принята, ТУ не переданы (К-8); вентканалы приняты, в брифе не заданы (К-9); подрайон климата не задан — принят не северный (жилые от 2,5 м) (К-10). Знак «*» — принято, не замерено и не подтверждено (замерить на объекте): К-1: дверь пом. 1 (стена В) — Петли у правого откоса (х 4600): открытое полотно стоит у стены Б, вошедший идёт влево к кухне; при петлях слева полотно запирало вход в карман между собой, диваном Гс2 и стеной Б; дверь пом. 2 (стена В) — проём в существующей стене между пом. 2 и 5: положение и ширина — по брифу заказчика, не замерены; К-4: Ст К1-1 — положение стояка канализации — по брифу заказчика, не замерено; Ст В1-1 — положение стояка холодной воды — по брифу заказчика, не замерено. Знак «**» — предложение проектировщика, заказчиком не утверждено (согласовать с заказчиком): плинтус пом. 1, 2, 5, фартук пом. 1 — артикул изделия не выбран: позиция описана характеристиками («аналог по характеристикам»), артикул выбирается при закупке; пол пом. 4 — пирог пола: стяжка 33 мм и обмазочная гидроизоляция добавлены разработчиком проекта; артикул изделия не выбран: позиция описана характеристиками («аналог по характеристикам»), артикул выбирается при закупке; К-5: дверь пом. 3 (стена Б), 4 (Г) — дверь в новой перегородке: проём по брифу, короб скрытой двери и размер в свету — после выбора модели и утверждения перегородки (К-5); П-1 — положение, материал (пеноблок) и толщина 100 мм — по брифу заказчика; конструкция (кладка, армирование, штукатурка) — выбор исполнителя, автором не утверждена; кладка — не ГКЛ: каркас, листы и Rw системы не считаются (система, лист, слои, Rw — «—»); П-2 — положение, материал (ГКЛ) и толщина 150 мм — по брифу заказчика; конструкция (система С112, 2 слоя с каждой стороны, Rw 51 дБ — нижняя граница диапазона системы С112 (51–56 дБ)) — выбор исполнителя, автором не утверждена; П-3 — положение, материал (кирпич) и толщина 120 мм — по брифу заказчика; конструкция (кладка, армирование, штукатурка) — выбор исполнителя, автором не утверждена; кладка — не ГКЛ: каркас, листы и Rw системы не считаются (система, лист, слои, Rw — «—»). См. лист открытых вопросов (лист 6, записи К-1–К-5, К-7–К-10).

Экспликация полов

Номер помещения	Тип пола	Схема пола	Данные элементов пола (наименование, толщина, основание), мм	Площадь, м²
1, 2, 3	1		Инженерная доска на клею — 14 Стяжка ЦПС М200 — 50 Плита перекрытия Всего 64 мм; ЧП ±0,000, верх плиты −0,064	42,98
4	2		Керамогранит на клею С2 TE S1 — 14 Гидроизоляция обмазочная, 2 слоя, с заведением на стены 200 мм — 2 Стяжка ЦПС М200 — 33 Плита перекрытия Всего 49 мм; ЧП −0,015, верх плиты −0,064	4,81
5	3		Керамогранит на клею С2 TE S1 — 14 Стяжка ЦПС М200 — 50 Плита перекрытия Всего 64 мм; ЧП ±0,000, верх плиты −0,064	8,58
			Итого	**56,37**

Раскладка покрытий

Пом.	Укладка	Старт (оси от чистовых стен), мм	Отступ 1-го ряда / крайние плитки, мм
1	вдоль стен А/В, прямая	от стены А, 1-й ряд вдоль неё	зазор от стены не задан
2	вдоль стен А/В, прямая	от стены А, 1-й ряд вдоль неё	зазор от стены не задан
3	вдоль стен А/В, прямая	от стены В, 1-й ряд вдоль неё	зазор от стены не задан
4	прямая, сетка 600×600, шов 2	ось X 901 от Г; ось Y 1276 от А	X 599 / 599; Y 372 / 372
5	плитка	раскладка плиточника не задана	

Стыки покрытий в проёмах

Марка	Проём	Типы пола	Отметки ЧП	Решение
СТ1	1–5 (Д-2)	1 / 3	±0,000 / ±0,000	Т-профиль
СТ2	2–5 (Д-3)	1 / 3	±0,000 / ±0,000	Т-профиль
СТ3	3–5 (Д-4)	1 / 3	±0,000 / ±0,000	Т-профиль
СТ4	4–5 (Д-5)	2 / 3	−0,015 / ±0,000	порог h=15 мм

Примечания

1. За отметку ±0,000 принят чистый пол, не существующий (блок отметок). Площади — по чистым размерам помещений, м²; размеры — в мм.
2. Стык разнотипных покрытий — по оси дверного полотна (под полотном в закрытом положении); решение стыка — по ведомости стыков.
3. Пол санузлов ниже смежных помещений на 15 мм за счёт меньшей толщины стяжки (верх плиты общий — по экспликации полов); гидроизоляция по стяжке с заведением на стены не менее 200 мм (СП 29.13330.2011, п. 7.2), до облицовки — тест проливом и акт скрытых работ.
4. Трубопроводы в конструкции пола не прокладываются: пирог пола 49–64 мм не вмещает выпуски канализации с уклоном — выпуски К1 ведутся по стенам над чистым полом в коробах (лист 44).
5. Звукоизоляционный слой под стяжкой проектом не предусмотрен (стяжка по плите): приведённый уровень ударного шума перекрытия с полом Lnw не более 60 дБ (СП 51.13330.2011, табл. 2) подтвердить по данным дома; при превышении — плавающая стяжка по звукоизоляции с демпферной лентой по контуру и у стояков, пирог пересчитать.
6. Штучные покрытия (инженерная доска): направление — по стрелке; влажность основания по СМ не более 2,0 % (по ТУ изготовителя).
7. Ровность основания — просвет под 2-метровой рейкой не более 2 мм: пом. 1, 2, 3 (инженерная доска), пом. 4, 5 (керамогранит); проверить до укладки покрытия (СП 71.13330.2017, табл. 8.5).
8. Сетка на плитке — условная, в размер формата; точка старта и раскладка — по листу раскладки плитки.
9. Узор покрытия (заливка-код типа пола) прерывается под надписями — площадями помещений и отметками чистого пола.
10. Пироги полов — по экспликации полов: слои сверху вниз, толщины в мм; гидроизоляция мокрых зон — в пироге и в ведомости отделки; схема пола — без масштаба.

1000 мм · печать 1:1

Изм.	Кол.уч	Лист	№ док.	Подп.	Дата
Разраб.		Кырлан А.С.			13.11.26
Пров.					
ГИП					
Н. контр.					
Утв.					

ГД-2026-011-АИ

Квартира 56 м²

ЖК «Северный парк», Москва

Дизайн-проект интерьера

Стадия	Лист	Листов
РП	60	119

План полов

М 1:75

Кырлан Александр Сергеевич

выпуск 13.11.2026 № eb7810814f · стр. 67 из 139

Ведомость отделки помещений

Потолки, стены, низ стен, полы · площади в м², длины в м · отметки в м

Ведомость отделки помещений (форма 1 прил. А ГОСТ 21.501-2018)

№	Наименование помещения	Потолок			Стены и перегородки			Низ стен (плинтус)			Пол		Примечание
		Вид отделки	Код цвета	S, м²	Вид отделки	Код цвета	S, м²	Вид отделки	Код цвета	L, м	Вид отделки	S, м²	
1	Гостиная-кухня 20,80 м²	ГКЛ по каркасу П113, отм. +2,600; +2,500; окраска, Tikkurila Euro Power 7, глубокоматовая, 2 слоя, подготовка Q3	Tikkurila F485	20,80	Окраска, Tikkurila Euro Power 7, колеровка по NCS, матовая, 2 слоя, подготовка Q3 Акцент — стена А: окраска, Farrow & Ball Modern Emulsion, матовая, 2 слоя, подготовка Q3 Фартук кухни (стена Г): облицовка керамогранитом, аналог: керамогранит под травертин, матовый, 1200×600×9 мм, клей C2 TE S1, затирка CG2WA	NCS S 0804-Y30R Farrow & Ball No. 298 по артикулу	30,61 10,82 1,82	Плинтус МДФ h=80 мм, аналог: МДФ под покраску 80×16	NCS S 0804-Y30R	17,5	Инженерная доска, 1167-1101, 2100×127 мм, на клею; тип 1, отм. ЧП ±0,000	20,80	Н стен 2600 (до потолка); матовая моющаяся, класс 1 EN 13300 — осознанно вместо полуматовой; плинтус в цвет: стены
2	Спальня 13,60 м²	ГКЛ по каркасу П113, отм. +2,500; +2,600; окраска, Tikkurila Euro Power 7, глубокоматовая, 2 слоя, подготовка Q3	Tikkurila F485	13,60	Окраска, Tikkurila Euro Power 7, колеровка по NCS, матовая, 2 слоя, подготовка Q3 Акцент — стена А: окраска, Tikkurila Euro Power 7, колеровка по NCS, матовая, 2 слоя, подготовка Q3	NCS S 0804-Y30R NCS S 5010-G70Y	21,86 6,33	Плинтус МДФ h=80 мм, аналог: МДФ под покраску 80×16	NCS S 0804-Y30R	13,9	Инженерная доска, 1167-1101, 2100×127 мм, на клею; тип 1, отм. ЧП ±0,000	13,60	Н стен 2500 (до потолка); за встроенной мебелью до потолка (4,75 м²) финишной отделки нет — подготовка и грунт под мебель; плинтус в цвет: стены
3	Детская 8,58 м²	ГКЛ по каркасу П113, отм. +2,500; +2,600; окраска, Tikkurila Euro Power 7, глубокоматовая, 2 слоя, подготовка Q3	Tikkurila F485	8,58	Окраска, Tikkurila Euro Power 7, колеровка по NCS, матовая, 2 слоя, подготовка Q3 Акцент — стена Г: окраска, Tikkurila Euro Power 7, матовая, 2 слоя, подготовка Q3	NCS S 0804-Y30R Tikkurila X447	19,29 6,50	Плинтус МДФ h=69 мм, SX165	NCS S 0804-Y30R	11,0	Инженерная доска, 1167-1101, 2100×127 мм, на клею; тип 1, отм. ЧП ±0,000	8,58	Н стен 2500 (до потолка); плинтус в цвет: стены
4	Санузел 4,81 м²	ГКЛВ по каркасу П113, отм. +2,600; окраска, Tikkurila Euro Power 7, матовая, 2 слоя, подготовка Q3	Tikkurila F485	4,81	Облицовка плиткой, A8UZ, 600×1200×9 мм, клей C2 TE S1, затирка CG2WA	Atlas Concorde A8UZ	19,93	нет			Аналог: керамогранит ректифицированный под травертин, матовый, 600×600×9 мм; тип 2, отм. ЧП −0,015	4,81	Н стен 2615 (до потолка); гидроизоляция обмазочная, 2 слоя, с заведением на стены 200 мм; над ванной — до 2000 и 300 мм за борт (по пирогу пола); тест проливом и акт скрытых работ
5	Прихожая 8,58 м²	ГКЛ по каркасу П113, отм. +2,600; окраска, Tikkurila Euro Power 7, глубокоматовая, 2 слоя, подготовка Q3	Tikkurila F485	8,58	Окраска, Tikkurila Euro Power 7, колеровка по NCS, матовая, 2 слоя, подготовка Q3	NCS S 0804-Y30R	17,49	Плинтус МДФ h=80 мм, аналог: МДФ под покраску 80×16	NCS S 0804-Y30R	7,5	Керамогранит, A8UZ, 600×1200×9 мм; тип 3, отм. ЧП ±0,000	8,58	Н стен 2600 (до потолка); за встроенной мебелью до потолка (4,16 м²) финишной отделки нет — подготовка и грунт под мебель; матовая моющаяся, класс 1 EN 13300 — осознанно вместо полуматовой; плинтус в цвет: стены
	Итого			**56,37**			**134,64**			**49,9**		**56,37**	

Допущения и предложения на листе

Основа листа: размеры помещений и положение проёмов введены заказчиком в брифе, на объекте не замерены (К-1); высота потолка 2700 мм — по брифу заказчика, не замерена (К-2); толщины стен приняты по брифу: наружные 200 мм, внутренние 150 мм — не обмерены (К-1); тип дома монолитный, перекрытие 200 мм — по брифу заказчика, документов нет (К-3); планировка (стены, проёмы, объединение кухни и гостиной, расширение санузла) — по брифу без обмера и плана БТИ (К-7); разрешённая мощность 10 кВт принята, ТУ не переданы (К-8); вентканалы приняты, в брифе не заданы (К-9); подрайон климата не задан — принят не северный (жилые от 2,5 м) (К-10).

Знак «**» — предложение проектировщика, заказчиком не утверждено (согласовать с заказчиком): плинтус пом. 1, 2, 5, фартук пом. 1 — артикул изделия не выбран: позиция описана характеристиками («аналог по характеристикам»), артикул выбирается при закупке; пол пом. 4 — пирог пола: стяжка 33 мм и обмазочная гидроизоляция добавлены разработчиком проекта; артикул изделия не выбран: позиция описана характеристиками («аналог по характеристикам»), артикул выбирается при закупке.

См. лист открытых вопросов (лист 6, записи К-1–К-3, К-7–К-10).

Примечания

1. Площади поверхностей — по чистым граням стен до отделки: стены = периметр × высоту от чистого пола помещения до низа потолка минус проёмы (облицовка плиткой — до верха облицовки); плинтус = периметр минус дверные проёмы; пол и потолок — по площади помещения. Количество плиток по раскладке. Площади помещений — с учётом всех частей помещения; откосы в площадь стен не входят.
2. Акцентные стены и фартук — отдельными строками, их площадь вычтена из основной отделки стен помещения; фартук — над нижними модулями кухни от столешницы до низа навесных шкафов, где шкафов нет — на 600 мм.
3. Плинтус — длина по периметру за вычетом дверных проёмов; примыкания к наличникам и встроенной мебели — по развёрткам.
4. Формат плитки — Ш×В×Т (ширина × высота в положении укладки × толщина), мм; на полу — вдоль стен А/В × вдоль стен Б/Г.
5. Коды цвета — по веерам производителей; колеровка каждой краски одной партией, проверка выкраса при свете D65 и при лампах проекта.
6. Уровни подготовки Q1–Q4 — система Knauf, не норма ГОСТ/СП; допуски поверхностей — по СП 71.13330.2017 (действующая редакция).
7. «аналог:» — изделие задано характеристиками, марку и артикул согласовать с заказчиком до закупки.
8. Сводка площадей по материалам, м²: потолок — Tikkurila F485 Euro Power 7 — 56,37; стены — NCS S 0804-Y30R Euro Power 7, колеровка по NCS 89,25; стены — Farrow & Ball No. 298 Modern Emulsion — 10,82; стены — NCS S 5010-G70Y Euro Power 7, колеровка по NCS — 6,33; стены — Tikkurila X447 Euro Power 7 — 6,50; стены — облицовка плиткой 600×1200×9 мм, Atlas Concorde A8UZ — 19,93; фартук — облицовка керамогранитом 1200×600×9 мм — 1,82.

Изм.	Кол.уч	Лист	№ док.	Подп.	Дата
Разраб.		Кырлан А.С.			13.11.26
Пров.					
ГИП					
Н. контр.					
Утв.					

ГД-2026-011-АИ

Квартира 56 м²

ЖК «Северный парк», Москва

Дизайн-проект интерьера

Стадия	Лист	Листов
РП	61	119

Ведомость отделки помещений

М б/м

Кырлан Александр Сергеевич

Колерная карта

Цвета и материалы по помещениям · палитра проекта · выкрасы на согласование

Колерная карта по помещениям

Помещение	Поверхность	Образец	Поз.	Система и код цвета	Производитель, линейка / материал, артикул	Блеск	Класс истирания	LRV	Площадь
1. Гостиная-кухня 20,8 м²	стены		**К1**	NCS S 0804-Y30R	Tikkurila · Euro Power 7, колеровка по NCS	матовая	1	78	30,6 м²
	акцент А		**К2**	Farrow & Ball No. 298	Farrow & Ball · Modern Emulsion	матовая	1	≈14	10,8 м²
	потолок		**К3**	Tikkurila F485	Tikkurila · Euro Power 7	глубокомат.	2	83	20,8 м²
	пол		**КМ1**	по образцу	Coswick · Классическая · арт. 1167-1101				20,8 м²
	плинтус		**К4**	NCS S 0804-Y30R	МДФ · в цвет NCS			78	17,5 м
	фартук		**КМ2**	по образцу	керамогранит · аналог по хар.				1,8 м²
2. Спальня 13,6 м²	стены		**К1**	NCS S 0804-Y30R	Tikkurila · Euro Power 7, колеровка по NCS	матовая	1	78	21,9 м²
	акцент А		**К5**	NCS S 5010-G70Y	Tikkurila · Euro Power 7, колеровка по NCS	матовая	1	22	6,3 м²
	потолок		**К3**	Tikkurila F485	Tikkurila · Euro Power 7	глубокомат.	2	83	13,6 м²
	пол		**КМ1**	по образцу	Coswick · Классическая · арт. 1167-1101				13,6 м²
	плинтус		**К4**	NCS S 0804-Y30R	МДФ · в цвет NCS			78	13,9 м
3. Детская 8,58 м²	стены		**К1**	NCS S 0804-Y30R	Tikkurila · Euro Power 7, колеровка по NCS	матовая	1	78	19,3 м²
	акцент Г		**К6**	Tikkurila X447	Tikkurila · Euro Power 7	матовая	1	63	6,5 м²
	потолок		**К3**	Tikkurila F485	Tikkurila · Euro Power 7	глубокомат.	2	83	8,6 м²
	пол		**КМ1**	по образцу	Coswick · Классическая · арт. 1167-1101				8,6 м²
	плинтус		**К7**	NCS S 0804-Y30R	Orac Decor · Contour (Luxxus)			78	11,0 м
4. Санузел 4,81 м²	стены		**КМ3**	Marvel Travertine	Atlas Concorde · арт. A8UZ				19,9 м²
	потолок		**К8**	Tikkurila F485	Tikkurila · Euro Power 7	матовая	1	83	4,8 м²
	пол		**КМ4**	по образцу	керамогранит · аналог по хар.				4,8 м²
5. Прихожая 8,58 м²	стены		**К1**	NCS S 0804-Y30R	Tikkurila · Euro Power 7, колеровка по NCS	матовая	1	78	17,5 м²
	потолок		**К3**	Tikkurila F485	Tikkurila · Euro Power 7	глубокомат.	2	83	8,6 м²
	пол		**КМ5**	Marvel Travertine	Atlas Concorde · арт. A8UZ				8,6 м²
	плинтус		**К4**	NCS S 0804-Y30R	МДФ · в цвет NCS			78	7,5 м

Перечень выкрасов на согласование

№	Код	Бренд / веер	Пом. / стена	Подложка	Формат	Статус
1	S 0804-Y30R	NCS Tikkurila	1, 2, 3, 5	ГКЛ с грунтом; МДФ под эмаль	600×1000; 300×600	к выполнению
2	No. 298	Farrow & Ball	1 А	ГКЛ с грунтом	600×1000	к выполнению
3	F485	Tikkurila	1, 2, 3, 4, 5	ГКЛ с грунтом	600×1000	к выполнению
4	S 5010-G70Y	NCS Tikkurila	2 А	ГКЛ с грунтом	600×1000	к выполнению
5	X447	Tikkurila	3 Г	ГКЛ с грунтом	600×1000	к выполнению

Схема квартиры: цвет стен и акценты (б/м)


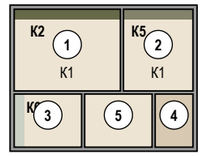


Схема палитры проекта


Стиль: Джапанди · схема: аналоговая

основной	основной	второстепенный	второстепенный	второстепенный	акцентный	акцентный	акцентный
NCS S 0804-Y30R	**Tikkurila F485**	**Tikkurila X447**	**Tikkurila V484**	**NCS S 2005-Y30R**	**Farrow & Ball No. 298**	**NCS S 5010-G70Y**	**NCS S 7005-Y20R**
светлый «рисовая бумага» LRV 78 стены 1,2,3,5; плинтус 1,2,3,5	Damask LRV 83 потолок 1,2,3,4,5; текстиль/декор 1,2,3,4	Sea Smoke LRV 63 акцент 3; текстиль/декор 1,2,3	Driftwood LRV 47 текстиль/декор 1,2,3	песочный грейж LRV 55 текстиль/декор 2,4	Bancha LRV ≈14 акцент 1; текстиль/декор 1	приглушённая олива LRV 22 акцент 2; текстиль/декор 2,4	тёмный орех LRV 9 в отделке не применён

План 60/30/10

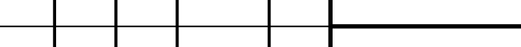

Окраска, факт — по площади стен, акцентов, потолков

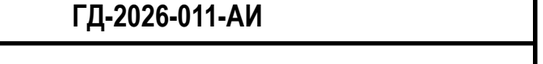

окрашено всего 169,3 м²; второстепенный тон несут мебель и текстиль

Текстиль и декор в цветах вне палитры проекта

NCS S 1002-Y50R тёплый светлый грейж — пом. 3 (Т10)

Условные обозначения

К1 NCS S 0804-Y30R · светлый «рисовая бумага» · Tikkurila Euro Power 7, колеровка по NCS · матовая · кл. 1

К2 Farrow & Ball No. 298 · Bancha · Modern Emulsion · матовая · кл. 1

К3 Tikkurila F485 · Damask · Euro Power 7 · глубокомат. · кл. 2

К4 NCS S 0804-Y30R · светлый «рисовая бумага» · МДФ

К5 NCS S 5010-G70Y · приглушённая олива · Tikkurila Euro Power 7, колеровка по NCS · матовая · кл. 1

К6 Tikkurila X447 · Sea Smoke · Euro Power 7 · матовая · кл. 1

К7 NCS S 0804-Y30R · светлый «рисовая бумага» · Orac Decor Contour (Luxxus)

К8 Tikkurila F485 · Damask · Euro Power 7 · матовая · кл. 1

дерево (доска, паркет, ламинат) — рисунок досок

керамогранит, плитка, камень — сетка швов по формату

КМ1 инженерная доска · 1167-1101

КМ2 аналог: керамогранит под травертин, матовый, 1200×600×9 мм

КМ3 плитка · A8UZ

КМ4 аналог: керамогранит ректифицированный под травертин, матовый, 600×600×9 мм

КМ5 керамогранит · A8UZ

К — краска, КМ — отделочный материал (тон КМ — по описанию, эталон — образец материала); кл. — класс истирания (1 — самый стойкий к мытью); LRV — светлота цвета: 0 — чёрный, 100 — белый; «≈» — ориентировочно

Примечания

1. Цвет на листе и на экране — ориентир. До покраски — выкрас на объекте: не меньше А3 (или лист ГКЛ), на грунте под эту краску, не на белой шпаклёвке, в 2 слоя; на обороте — код, бренд, веер, дата. Смотреть днём и вечером, рядом с образцами пола и плитки; к основному цвету стен — ещё 2 соседних оттенка. Красить только в цвет утверждённого выкраса.
2. Краску заказывать по коду из графы «Система и код цвета» у бренда этого кода, не «аналогом» другого; весь объём одного кода — одной партией, колеруемую краску — за один проход машины.
3. Площади — те же, что в ведомости отделки (лист 61); сколько краски заказать — в спецификации отделочных материалов (лист 63).

Допущения и предложения на листе. Основа листа: размеры помещений и положение проёмов введены заказчиком в брифе, на объекте не замерены (К-1); высота потолка 2700 мм — по брифу заказчика, не замерена (К-2); толщины стен приняты по брифу: наружные 200 мм, внутренние 150 мм — не обмерены (К-1); тип дома монолитный, перекрытие 200 мм — по брифу заказчика, документов нет (К-3); планировка (стены, проёмы, объединение кухни и гостиной, расширение санузла) — по брифу без обмера и плана БТИ (К-7); разрешённая мощность 10 кВт принята, ТУ не переданы (К-8); вентканалы приняты, в брифе не заданы (К-9); подрайон климата не задан — принят не северный (жилые от 2,5 м) (К-10). Знак «**» — предложение проектировщика, заказчиком не утверждено (согласовать с заказчиком): плинтус пом. 1, 2, 5, фартук пом. 1 — артикул изделия не выбран: позиция описана характеристиками («аналог по характеристикам»), артикул выбирается при закупке; пол пом. 4 — пирог пола: стяжка 33 мм и обмазочная гидроизоляция добавлены разработчиком проекта; артикул изделия не выбран: позиция описана характеристиками («аналог по характеристикам»), артикул выбирается при закупке. См. лист открытых вопросов (лист 6, записи К-1–К-3, К-6–К-10); по листу — К-6.

Изм.	Кол.уч	Лист	№ док.	Подп.	Дата
Разраб.		Кырлан А.С.			13.11.26
Пров.					
ГИП					
Н. контр.					
Утв.					

ГД-2026-011-АИ

Квартира 56 м²

ЖК «Северный парк», Москва

Дизайн-проект интерьера

Стадия	Лист	Листов
РП	62	119

Колерная карта

М б/м

Кырлан Александр Сергеевич

выпуск 13.11.2026 № eb7810814f · стр. 69 из 139

Спецификация отделочных материалов

ПРЕДВАРИТЕЛЬНО · не для производства работ · открыто пунктов: 13 (реестр — л. 6, 7)

Форма 1 по ГОСТ 21.110-2013 · количества — из геометрии проекта, с запасом

Поз.	Наименование и техническая характеристика	Тип, марка, обозначение документа	Код продукции	Поставщик	Ед. изм.	Кол.	Масса 1 ед., кг	Примечание
	Лакокрасочные материалы							
1	Краска интерьерная водно-дисперсионная акриловая для стен, матовая, класс мокрого истирания 1 по EN 13300, база A; цвет NCS S 0804-Y30R «S 0804-Y30R», колеровка машинная	Tikkurila Euro Power 7, колеровка по NCS		Tikkurila	л	24,3		поз. К1 колерной карты; пом. 1, 2, 3, 5; S = 89,2 м² × 2 сл. × 0,12 л/м² = 21,4 л, +10 % и 0,5 л на подкраску → ≥ 24,1 л; тара 2 × 9 л + 2 × 2,7 л + 1 × 0,9 л
2	Краска интерьерная водно-дисперсионная акриловая для акцентных стен, матовая, класс мокрого истирания 1 по EN 13300, база C; цвет по вееру Farrow & Ball No. 298 «Bancha», колеровка машинная	Farrow & Ball Modern Emulsion		Farrow & Ball	л	5		поз. К2 колерной карты; пом. 1; S = 10,8 м² × 2 сл. × 0,12 л/м² = 2,6 л, +10 % и 0,5 л на подкраску → ≥ 3,4 л; тара 1 × 5 л
3	Краска интерьерная водно-дисперсионная акриловая для потолков, глубокоматовая, класс мокрого истирания 2 по EN 13300, база A; цвет по вееру Tikkurila F485 «Damask», колеровка машинная	Tikkurila Euro Power 7		Tikkurila	л	14,4		поз. К3 колерной карты; пом. 1, 2, 3, 5; S = 51,6 м² × 2 сл. × 0,12 л/м² = 12,4 л, +10 % и 0,5 л на подкраску → ≥ 14,1 л; тара 1 × 9 л + 2 × 2,7 л
4	Краска интерьерная водно-дисперсионная акриловая для акцентных стен, матовая, класс мокрого истирания 1 по EN 13300, база C; цвет NCS S 5010-G70Y «S 5010-G70Y», колеровка машинная	Tikkurila Euro Power 7, колеровка по NCS		Tikkurila	л	2,7		поз. К5 колерной карты; пом. 2; S = 6,3 м² × 2 сл. × 0,12 л/м² = 1,5 л, +10 % и 0,5 л на подкраску → ≥ 2,2 л; тара 1 × 2,7 л
5	Краска интерьерная водно-дисперсионная акриловая для акцентных стен, матовая, класс мокрого истирания 1 по EN 13300, база C; цвет по вееру Tikkurila X447 «Sea Smoke», колеровка машинная	Tikkurila Euro Power 7		Tikkurila	л	2,7		поз. К6 колерной карты; пом. 3; S = 6,5 м² × 2 сл. × 0,12 л/м² = 1,6 л, +10 % и 0,5 л на подкраску → ≥ 2,2 л; тара 1 × 2,7 л
6	Краска интерьерная водно-дисперсионная акриловая для потолков, матовая, класс мокрого истирания 1 по EN 13300, база A; цвет по вееру Tikkurila F485 «Damask», колеровка машинная	Tikkurila Euro Power 7		Tikkurila	л	1,8		поз. К8 колерной карты; пом. 4; S = 4,8 м² × 2 сл. × 0,12 л/м² = 1,2 л, +10 % и 0,5 л на подкраску → ≥ 1,8 л; тара 2 × 0,9 л
7	Краска для МДФ и дерева в цвет NCS S 0804-Y30R «S 0804-Y30R» — окраска плинтуса; блеск не ниже блеска стен	марка не задана			л	1,3		поз. К4, К7; пом. 1, 2, 3, 5; L = 49,9 м, S = 4,7 м² × 2 сл. × 0,12 л/м² + 10 %; продукт подобрать в веере NCS
8	Грунтовка акриловая под окраску стен и потолков — из системы производителя краски	по системе краски			м²	170		площадь окраски стен, акцентов и потолков; 1 слой перед окраской; расход — по ТУ грунтовки
	Плитка и керамогранит							
9	Керамогранит под травертин, 600×600×9 мм, ректификат, водопоглощение 0,1 % (BIa), противоскольжение R10, PEI IV	аналог по характеристикам			м²	6,12		шов 2 мм; Санузел, пол; по раскладке 15 шт (S = 4,81 м²), с запасом 17 шт
10	A8UZ, 600×1200×9 мм, ректификат, водопоглощение 0,1 % (BIa), противоскольжение R10, PEI IV	A8UZ		Atlas Concorde	м²	45,36		шов 2 мм; Санузел, стены А–Г; Санузел, короб инсталляции; Прихожая, пол; по раскладке 56 шт (S = 29,31 м²), с запасом 63 шт
11	Керамогранит под травертин, матовый, 1200×600×9 мм, ректификат, водопоглощение 0,1 % (BIa)	аналог по характеристикам			м²	4,32		шов 2 мм; Гостиная-кухня, фартук (ст. Г); по раскладке 5 шт (S = 1,82 м²), с запасом 6 шт
	Напольные покрытия							
12	1167-1101, рабочий слой 4 мм, эмиссия E1, укладка на клей	1167-1101		Coswick	м²	46,2		пом. 1, 2, 3; S = 43,18 м² (пол + половина стены в дверных проёмах, как в смете) + 7 %; к заказу — кратно упаковке
13	Клей для паркета и инженерной доски, эластичный (СМП / полиуретановый)	по рекомендации производителя доски			м²	44		площадь приклейки; расход и шпатель — по ТУ клея
	Погонажные изделия							
14	Плинтус МДФ под покраску 80×16, крепление к стене, окраска в цвет NCS S 0804-Y30R	аналог по характеристикам			м	43		пом. 1, 2, 5; L = 38,9 м (периметр без дверных проёмов) + 10 % на подрезку; в штуках — по длине планки
15	SX165, h = 69 мм, крепление к стене, окраска в цвет NCS S 0804-Y30R	SX165		Orac Decor	м	13		пом. 3; L = 11,0 м (периметр без дверных проёмов) + 10 % на подрезку; в штуках — по длине планки
	Смеси и материалы для облицовки							
16	Затирка для швов плитки, класс CG2WA по EN 13888	Mapei Ultracolor Plus 132		Mapei	кг	2,9		по раскладке (a+b)/(a·b) × шов × t × 1,6 + 10 %; в т. ч. 0,8 кг — позиции раскладки без марки
17	Клей плиточный C2 TE S1 по EN 12004, слой 5 мм	Ceresit CM 17		Ceresit	кг	231		10 меш. по 25 кг; 1,5 кг/м² на 1 мм слоя + 10 %; в т. ч. 68 кг — позиции раскладки без марки
18	Гидроизоляция обмазочная мокрых зон: пол, стены по периметру, зоны замачивания; 2 слоя с армирующей лентой в углах	аналог по характеристикам			м²	12,4		площадь по листу раскладки плитки + 10 %; расход смеси — по ТУ
19	Лента демпферная по периметру пола из плитки	аналог по характеристикам			м	16,9		периметр без дверных проёмов + 10 %

Примечания

1. Количества — из геометрии проекта: площади поверхностей по чистым граням стен до отделки (те же, что в ведомости отделки и колерной карте), плитка, клей и затирка — по раскладке плиточника; в графе «Кол.» — к заказу, с запасом.
2. Краска: расход 0,12 л/м² на слой в 2 слоя, если по ТУ не задан иной; запас 10 % и 0,5 л на подкраску каждого кода. Один код — одна партия, колеровка машинная в колеровочном центре бренда; в заказ — только после утверждения выкраса (колерная карта). Фасовка — по каталогу бренда на дату выпуска; к заказу — не меньше расчётного объёма.
3. «Аналог по характеристикам» — допускается изделие другого производителя с характеристиками не ниже указанных, по согласованию с автором проекта.
4. Графы «Код продукции» и «Масса 1 ед.» не заполнены: коды по классификатору продукции не присвоены, масса единицы до 25 кг (ГОСТ 21.110-2013).
5. Грунтовка и клей для доски указаны площадью обработки; объём — по ТУ выбранного продукта.

Допущения и предложения на листе

Основа листа: размеры помещений и положение проёмов введены заказчиком в брифе, на объекте не замерены (К-1); высота потолка 2700 мм — по брифу заказчика, не замерена (К-2); толщины стен приняты по брифу: наружные 200 мм, внутренние 150 мм — не обмерены (К-1); тип дома монолитный, перекрытие 200 мм — по брифу заказчика, документов нет (К-3); планировка (стены, проёмы, объединение кухни и гостиной, расширение санузла) — по брифу без обмера и плана БТИ (К-7); разрешённая мощность 10 кВт принята, ТУ не переданы (К-8); вентканалы приняты, в брифе не заданы (К-9); подрайон климата не задан — принят не северный (жилые от 2,5 м) (К-10).

Знак «**» — предложение проектировщика, заказчиком не утверждено (согласовать с заказчиком): плинтус пом. 1, 2, 5, фартук пом. 1 — артикул изделия не выбран: позиция описана характеристиками («аналог по характеристикам»), артикул выбирается при закупке; пол пом. 4 — пирог пола: стяжка 33 мм и обмазочная гидроизоляция добавлены разработчиком проекта; артикул изделия не выбран: позиция описана характеристиками («аналог по характеристикам»), артикул выбирается при закупке.

См. лист открытых вопросов (лист 6, записи К-1–К-3, К-7–К-10).

Изм.	Кол.уч	Лист	№ док.	Подп.	Дата
Разраб.		Кырлан А.С.			13.11.26
Пров.					
ГИП					
Н. контр.					
Утв.					

ГД-2026-011-АИ

Квартира 56 м²

ЖК «Северный парк», Москва

Дизайн-проект интерьера	Стадия	Лист	Листов
	РП	63	119

Спецификация отделочных материалов

М б/м

Кырлан Александр Сергеевич

Концепция декора и визуализации

Джапанди · джапанди · визуализации, палитра, материалы, ключевые предметы



Визуализация 1. Вид сверху (3D): планировка с мебелью, текстилем и декором

Расстановка — по плану мебели (лист 27); шторы, ковры, картины и растения — по плану текстиля и декора (лист 65).



Визуализация 15. Гостиная-кухня (пом. 1)

шторы Т13, Т14 · ковёр Т16 · картина ДК6 · растение ДК7 · подушки, пледы Т17, Т18, Т19



Визуализация 8. Спальня (пом. 2)

шторы Т1, Т2 · ковёр Т3 · картина ДК1 · растение ДК16** · подушки, пледы Т4, Т5, Т6



Визуализация 12. Детская (пом. 3)

шторы Т7, Т8 · ковёр Т9 · картина ДК3 · зеркало ДК4 · подушки, пледы Т10, Т11, Т12



Визуализация 6. Санузел (пом. 4)

ковёр Т22** · зеркало ДК2 · подушки, пледы Т20**, Т21**

Палитра 60/30/10 и цвета текстиля



- NCS S 0804-Y30R (светлый «рисовая бумага»), LRV 78 — 60 % база
- Tikkurila X447 (Sea Smoke), LRV 63 — 30 % второй цвет — Т1, Т4, Т7, Т11, Т12, Т13, Т17
- NCS S 2005-Y30R (песочный грейж), LRV 55 — 30 % второй цвет — Т3, Т22
- NCS S 5010-G70Y (приглушённая олива), LRV 22 — 10 % акцент — Т5, Т6, Т20
- NCS S 1002-Y50R (тёплый светлый грейж), LRV 74 — текстиль — Т10
- Tikkurila F485 (Damask), LRV 83 — 60 % база — Т2, Т8, Т14, Т21
- Tikkurila V484 (Driftwood), LRV 47 — 30 % второй цвет — Т9, Т16, Т19
- Farrow & Ball No. 298 (Bancha), LRV 14 — 10 % акцент — Т18
- NCS S 7005-Y20R (тёмный орех), LRV 9 — 10 % акцент

Материалы и фактуры



Дуб натуральный

пол: пом. 1, 2, 3; рамы ДК1, ДК3, ДК10**



Травертин (керамогранит)

пол и стены санузлов, фартук: пом. 1, 4



Букле

подушки: Т10, Т17



Лён

портьеры, подушки, полотенца: Т1, Т4, Т7, Т13, Т20**, Т21**



Бронза и чёрный металл

рамы ДК4, ДК5 — чёрный; фурнитура, светильники — бронза

Ключевые предметы

— Диван Гс2 2000×900 — гостиная-кухня; подушки и плед Т17, Т18, Т19

— Кровати Дт1, Сп1 — над изголовьем картины ДК1, ДК3; текстиль Т4, Т5, Т6, Т10, Т11, Т12

— Ковры Т3, Т9, Т16, Т22** — шерсть, хлопок тафтинг, на противоскользящей подложке

— Картины ДК1, ДК3, ДК6, ДК10** — центр на высоте 1200–1550 мм

— Зеркала в рост ДК4; над умывальниками ДК2, ДК5

— Шторы-волна Т1, Т7, Т13 (Tikkurila X447), тюль Т2, Т8, Т14 (Tikkurila F485) — в нишах потолка

— Растение ДК7, ваза ДК8, растение ДК16**, ваза ДК9**

Настроение

Джапанди по брифу: стены S 0804-Y30R, потолок Damask F485, серо-зелёный Sea Smoke и дуб под маслом, акценты — олива Bancha и тёмный орех; без глянца (К-6). Настроение стиля: тишина, заземлённость, медленная жизнь, тёплый минимализм, ваби-саби, hygge. Свет тёплый, 2200–3000 К.

Примечания

1. Визуализации — образ интерьера. Изделия, размеры, высоты подвеса и привязки — по чертежам (план текстиля и декора — лист 65; шторы и карнизы — лист 66; ведомость текстиля — лист 67; ведомость декора и развеска — лист 68); при расхождении действуют чертежи и ведомости.
2. Коды цвета — ориентир подбора по веерам производителей; ткань утверждается по образцу при дневном свете и при свете проекта 2700–3000 К.
3. Мелкий стайлинг на визуализациях (книги, посуда, свечи) в ведомости не входит и поставляется заказчиком по желанию.

Допущения и предложения на листе. Знак «**» предложено (согласовать). См. лист открытых вопросов (листы 6, 7).

Изм.	Кол.уч	Лист	№ док.	Подп.	Дата
Разраб.		Кырлан А.С.			13.11.26
Пров.					
ГИП					
Н. контр.					
Утв.					

ГД-2026-011-АИ

Квартира 56 м²

ЖК «Северный парк», Москва

Дизайн-проект интерьера

Стадия	Лист	Листов
РП	64	119

Концепция декора и визуализации

М б/м


Кырлан Александр Сергеевич

выпуск 13.11.2026 № eb7810814f · стр. 71 из 139

План текстиля и декора

Шторы и карнизы, ковры, картины и зеркала, растения · размеры в мм от чистовых стен и чистого пола · марки — по ведомостям

ПРЕДВАРИТЕЛЬНО · не для производства работ · открыто пунктов: 13 (реестр — л. 6, 7)

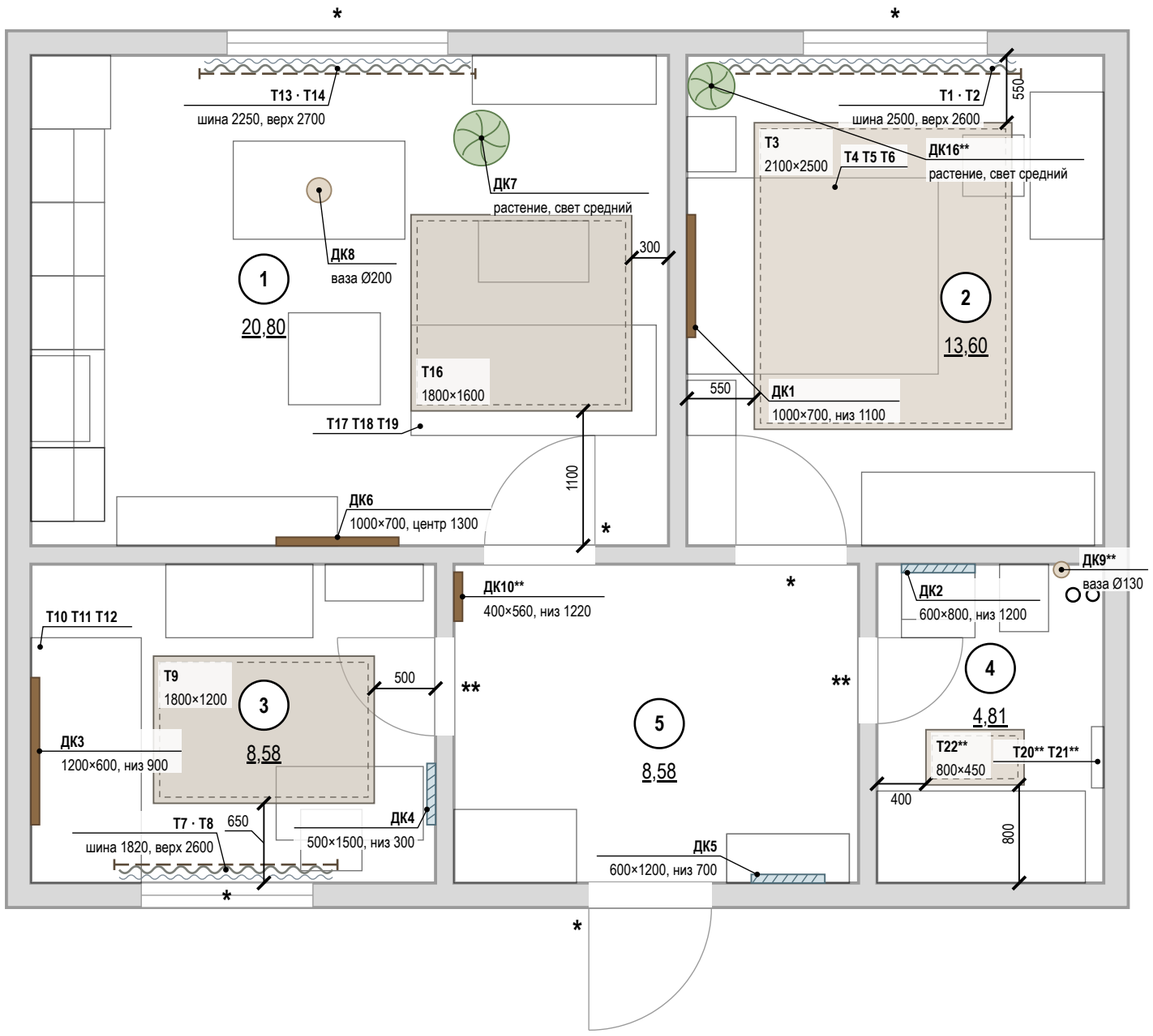

Допущения и предложения на листе. Основа листа: размеры помещений и положение проёмов введены заказчиком в брифе, на объекте не замерены (К-1); высота потолка 2700 мм — по брифу заказчика, не замерена (К-2); толщины стен приняты по брифу: наружные 200 мм, внутренние 150 мм — не обмерены (К-1); тип дома монолитный, перекрытие 200 мм — по брифу заказчика, документов нет (К-3); планировка (стены, проёмы, объединение кухни и гостиной, расширение санузла) — по брифу без обмера и плана БТИ (К-7); разрешённая мощность 10 кВт принята, ТУ не переданы (К-8); вентканалы приняты, в брифе не заданы (К-9); подрайон климата не задан — принят не северный (жилые от 2,5 м) (К-10). Знак «*» — принято, не замерено и не подтверждено (замерить на объекте): К-4: Ст К1-1 — положение стояка канализации — по брифу заказчика, не замерено; Ст В1-1 — положение стояка холодной воды — по брифу заказчика, не замерено. Знак «**» — предложение проектировщика, заказчиком не утверждено (согласовать с заказчиком). См. лист открытых вопросов (лист 6, записи К-1–К-5, К-7–К-10; лист 7, запись ИЗ-3); по листу — ИЗ-3.

Примечания

1. Размеры — в мм. Отступы ковров — от чистовых стен; высоты картин и зеркал — от чистого пола до центра или низа рамы.
2. Шторы в пол — на шинах в нишах потолка (ниша — план потолков, лист 53); закладная под шину в нише — до обшивки ГКЛ. Схемы окон, длины полотен и сборка лист 66.
3. Картины и зеркала массой более 5 кг — на анкеры по основанию, нагрузка крепежа не меньше двойной массы изделия; на ГКЛ — только по закладной. Декор не перекрывает розетки и выключатели.
4. Ковры на гладком полу — на противоскользящей подложке.
5. Мебель — по плану расстановки мебели (лист 27); ведомость текстиля — лист 67, ведомость декора и схемы развески — лист 68.
6. Знак «*» у проёма — допущение: положение проёма не замерено (окно пом. 1, стена А; дверь пом. 1, стена В; окно пом. 2, стена А; дверь пом. 2, стена В; окно пом. 3, стена В; дверь пом. 5, стена В); размер напечатан как принятый. Реестр: листы 6–7, вопросы К-1, К-11.
7. Номера помещений — по экспликации (лист 21); наименования и площади на этом листе не дублируются.
8. Марки текстиля «Т» и декора «Д» относятся только к листам текстиля и декора; индексы трубопроводов Т1–Т4 — на листах ВК и ОВ.

1000 мм · печать 1:1

Условные обозначения

- ковёр — габарит в масштабе, цвет изделия
- шина или карниз штор (выше плоскости разреза)
- портьеры (штора-волна)
- тюль (на плане — волнистая линия)
- римская или рулонная штора в проёме
- картина на стене — ширина в масштабе
- зеркало на стене — ширина в масштабе
- растение в кашпо — диаметр в масштабе
- ваза, настольный декор
- подушки, пледы — марка на выноске к своей мебели
- привязка от чистовой стены, мм
- (1) номер помещения, площадь м²
- стены (подложка обмера)
- * «*» — принято, не замерено и не подтверждено
- ** «**» — предложение проектировщика, заказчиком не утверждено

Т1, ДК1 — марки по ведомостям текстиля и декора

Экспликация помещений

лист 21 · на плане — номера в марках

Окна: шина → полотно, мм

Поз.	Шина	Верх шины	Полотно, низ
Т13, Т14	2250	2700, ниша	2690, низ 10
Т1, Т2	2500	2600, ниша	2590, низ 10
Т7, Т8	1820	2600, ниша	2590, низ 10

Развеска: высоты от пола, мм

Поз.	Пом.	Ш×В	Центр	Низ	Стена
ДК1	2	1000×700	1450	1100	Г
ДК2	4	600×800	1600	1200	А
ДК3	3	1200×600	1200	900	Г
ДК4	3	500×1500	1050	300	Б
ДК5	5	600×1200	1300	700	В
ДК6	1	1000×700	1300	950	В
ДК10**	5	400×560	1500	1220	Г

Изм.	Кол.уч	Лист	№ док.	Подп.	Дата
Разраб.		Кырлан А.С.			13.11.26
Пров.					
ГИП					
Н. контр.					
Утв.					

ГД-2026-011-АИ

Квартира 56 м²

ЖК «Северный парк», Москва

Дизайн-проект интерьера

Стадия	Лист	Листов
РП	65	119

План текстиля и декора

М 1:50

Кырлан Александр Сергеевич

выпуск 13.11.2026 № eb7810814f · стр. 72 из 139

08

Декор и текстиль


Кырлан Александр Сергеевич

выпуск 13.11.2026 · eb78110814f · стр. 73 из 139


Шторы и карнизы

Схемы окон «шина → полотно» (М 1:50) · отметки от чистого пола помещения · размеры в мм


Окно 1* — Гостиная-кухня (пом. 1): Т13, Т14 (М 1:50)

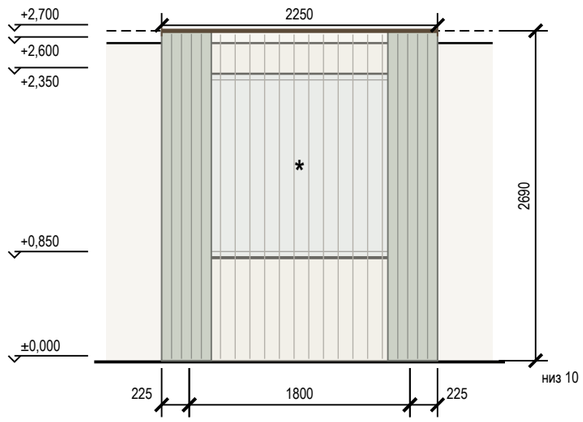

Окно 1* — Спальня (пом. 2): Т1, Т2 (М 1:50)

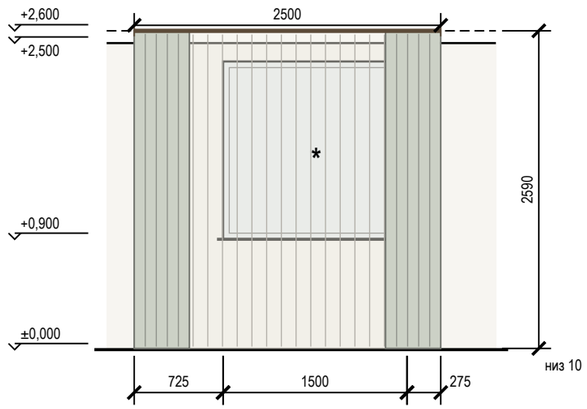

Окно 1* — Детская (пом. 3): Т7, Т8 (М 1:50)

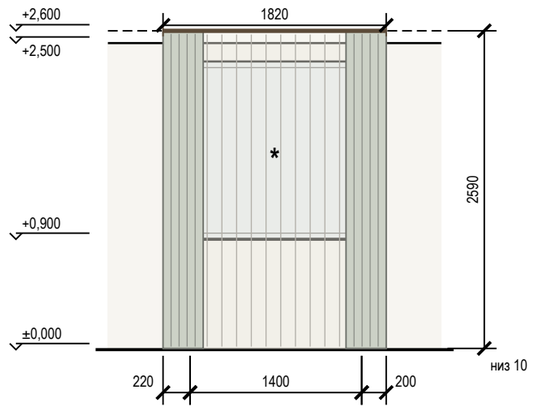

Карта окон: окно → шина → полотно

Поз.	Окно, пом.	Проём Ш×В, подоконник	Верх ниши	Изделие	Шина / карниз: длина, крепление	Верх шины	Полотно: длина, низ	Управление
Т13	1*, пом. 1	1800×1500, подок. 850	+2,700	портьеры	шина, 2250, в нише потолка, вынос 150	+2,700	2690, низ 10 (парит)	вручную
Т14	1*, пом. 1	1800×1500, подок. 850	+2,700	тюль	шина, 2250, в нише потолка, вынос 150	+2,700	2690, низ 10 (парит)	вручную
Т1	1*, пом. 2	1500×1450, подок. 900	+2,600	портьеры	шина, 2500, в нише потолка, вынос 150	+2,600	2590, низ 10 (парит)	вручную
Т2	1*, пом. 2	1500×1450, подок. 900	+2,600	тюль	шина, 2500, в нише потолка, вынос 150	+2,600	2590, низ 10 (парит)	вручную
Т7	1*, пом. 3	1400×1450, подок. 900	+2,600	портьеры	шина, 1820, в нише потолка, вынос 150	+2,600	2590, низ 10 (парит)	вручную
Т8	1*, пом. 3	1400×1450, подок. 900	+2,600	тюль	шина, 1820, в нише потолка, вынос 150	+2,600	2590, низ 10 (парит)	вручную

Задания смежникам

Кому	Задание	Пом.
Гипсокартонщик	окно 1 (1800×1500, Т13, Т14): ниша под шторы 150×100, верх +2,700; закладная под шину L 2250 по всей длине — до обшивки	1
Гипсокартонщик	окно 1 (1500×1450, Т1, Т2): ниша под шторы 150×100, верх +2,600; закладная под шину L 2500 по всей длине — до обшивки	2
Гипсокартонщик	окно 1 (1400×1450, Т7, Т8): ниша под шторы 150×100, верх +2,600; закладная под шину L 1820 по всей длине — до обшивки	3
Электрик	выводы под электрокарнизы не требуются (управление вручную)	

Условные обозначения

- портьеры в открытом положении
- римская штора: сложена / опущена
- верх ниши под шторы в потолке
- `*` — «*» — принято, не замерено и не подтверждено
- тюль (на виде окна — прозрачная плашка)
- шина или карниз на отметке верха
- оконный проём

Допущения и предложения на листе

Основа листа: размеры помещений и положение проёмов введены заказчиком в брифе, на объекте не замерены (К-1); высота потолка 2700 мм — по брифу заказчика, не замерена (К-2); толщины стен приняты по брифу: наружные 200 мм, внутренние 150 мм — не обмерены (К-1); тип дома монолитный, перекрытие 200 мм — по брифу заказчика, документов нет (К-3); планировка (стены, проёмы, объединение кухни и гостиной, расширение санузла) — по брифу без обмера и плана БТИ (К-7); разрешённая мощность 10 кВт принята, ТУ не переданы (К-8); вентканалы приняты, в брифе не заданы (К-9); подрайон климата не задан — принят не северный (жилые от 2,5 м) (К-10).

Знак «*» — принято, не замерено и не подтверждено (замерить на объекте): К-1: окно пом. 1 (стена А) — окно: положение, ширина, высота и подоконник — по брифу заказчика, не замерены; ограждение 900 мм — предложение исполнителя; дверь пом. 1 (стена В) — Петли у правого откоса (х 4600): открытое полотно стоит у стены Б, вошедший идёт влево к кухне; при петлях слева полотно запирало вход в карман между собой, диваном Гс2 и стеной Б; окно пом. 2 (стена А), 3 (В) — окно: положение, ширина, высота и подоконник — по брифу заказчика, не замерены; дверь пом. 2 (стена В) — проём в существующей стене между пом. 2 и 5: положение и ширина — по брифу заказчика, не замерены.

Знак «**» — предложение проектировщика, заказчиком не утверждено (согласовать с заказчиком): К-5: дверь пом. 3 (стена Б) — дверь в новой перегородке: проём по брифу, короб скрытой двери и размер в свету — после выбора модели и утверждения перегородки (К-5).

См. лист открытых вопросов (лист 6, записи К-1–К-3, К-5, К-7–К-10).

Примечания

1. Отметки — от чистого пола помещения; размеры — мм.
2. Шины в нишах потолка: закладная (брус или профиль) по всей длине ниши — до обшивки ГКЛ; ниша и её отметка — узел ниши на плане потолков (лист 53).
3. Шина в нише — на отметке верха ниши (крепление к закладной в потолке ниши); длина полотна — от верха шины до чистого пола за вычетом зазора.
4. Полотно портьер «парит» над полом на 10 мм; сборка портьер — 2,0, тюля — 2,5 (ширина полотна — в ведомости текстиля).
5. Электрокарнизы не предусмотрены; при замене на электропривод — вывод кабеля в нише у края шины (задание электрику).
6. Знак «*» у проёма — допущение: положение проёма не замерено (окно пом. 1, стена А; окно пом. 2, стена А; окно пом. 3, стена В); размер напечатан как принятый. Реестр: листы 6–7, вопрос К-1.
7. Длины шин и полотен окон 1 (пом. 1), 1 (пом. 2), 1 (пом. 3) выведены из размеров и положения проёма, а они — допущение: до раскроя полотен проём замерить, длины сверить.
8. Марки изделий — по плану текстиля и декора (лист 65) и ведомости текстиля (лист 67).

Изм.	Кол.уч	Лист	№ док.	Подп.	Дата
Разраб.		Кырлан А.С.			13.11.26
Пров.					
ГИП					
Н. контр.					
Утв.					

ГД-2026-011-АИ

Квартира 56 м²

ЖК «Северный парк», Москва

Дизайн-проект интерьера

Стадия	Лист	Листов
РП	66	119

Шторы и карнизы

М б/м

Кырлан Александр Сергеевич

выпуск 13.11.2026 № eb7810814f · стр. 74 из 139

Ведомость текстиля

Шторы, тюль, римские шторы, ковры, подушки и пледы · размеры в мм · марки — по плану текстиля и декора

ПРЕДВАРИТЕЛЬНО · не для производства работ · открыто пунктов: 13 (реестр — л. 6, 7)

Текстиль: шторы, ковры, подушки, пледы


Поз.	Пом.	Изделие	Размер, мм	Ткань, состав, плотность	Сборка, ширина полотна		Цвет (система, код)	Кол.	Примечание
T1	2	Портьеры-волна	шина 2500 × полотно 2590	лён с блэкаут-подкладкой; лён 100 %; 320 г/м²	× 2, ширина 5000		Tikkurila X447 (Sea Smoke)	2	низ 10 (парит); в нише потолка
T2	2	Тюль	шина 2500 × полотно 2590	вуаль; полиэстер 100 %	× 2,5, ширина 6250		Tikkurila F485 (Damask)	1	низ 10 (парит); в нише потолка
T3	2	Ковёр под кроватью, шерсть	2100×2500	шерсть, ручное ткачество; шерсть 80 %, хлопок 20 %			NCS S 2005-Y30R (песочный грейж)	1	противоскользящая подложка; ворс 10 мм
T4	2	Подушки декоративные на кровать	500×500	лён 100 %			Tikkurila X447 (Sea Smoke)	2	на Сп1
T5	2	Подушки на кровать, акцент	400×600	хлопковый бархат 100 %			NCS S 5010-G70Y (приглушённая олива)	2	на Сп1
T6	2	Плед на кровать	1300×1700	шерсть мериноса 100 %			NCS S 5010-G70Y (приглушённая олива)	1	на Сп1
T7	3	Портьеры-волна	шина 1820 × полотно 2590	лён с блэкаут-подкладкой; лён 100 %; 320 г/м²	× 2, ширина 3640		Tikkurila X447 (Sea Smoke)	2	низ 10 (парит); в нише потолка
T8	3	Тюль	шина 1820 × полотно 2590	вуаль; полиэстер 100 %	× 2,5, ширина 4550		Tikkurila F485 (Damask)	1	низ 10 (парит); в нише потолка
T9	3	Ковёр игровой, шерсть	1800×1200	шерсть, плоское плетение; шерсть 100 %			Tikkurila V484 (Driftwood)	1	противоскользящая подложка; ворс 8 мм
T10	3	Подушки декоративные на кровать	500×500	букле (шерсть 60 %, полиэстер 40 %)			NCS S 1002-Y50R (тёплый светлый грейж)	2	на Дт1
T11	3	Подушки на кровать, акцент	400×600	хлопковый бархат 100 %			Tikkurila X447 (Sea Smoke)	2	на Дт1
T12	3	Плед на кровать	1300×1700	шерсть мериноса 100 %			Tikkurila X447 (Sea Smoke)	1	на Дт1
T13	1	Портьеры-волна (гостиная)	шина 2250 × полотно 2690	лён 70 %, вискоза 30 %; 280 г/м²	× 2, ширина 4500		Tikkurila X447 (Sea Smoke)	2	низ 10 (парит); в нише потолка
T14	1	Тюль (гостиная)	шина 2250 × полотно 2690	вуаль; полиэстер 100 %	× 2,5, ширина 5625		Tikkurila F485 (Damask)	1	низ 10 (парит); в нише потолка
T16	1	Ковёр в зоне отдыха, джут с шерстью	1800×1600	шерсть, петля; шерсть 100 %			Tikkurila V484 (Driftwood)	1	противоскользящая подложка; ворс низкий
T17	1	Подушки на диван	500×500	букле (шерсть 60 %, полиэстер 40 %)			Tikkurila X447 (Sea Smoke)	2	на Гс2
T18	1	Подушки на диван, акцент	400×600	хлопковый бархат 100 %			Farrow & Ball No. 298 (Bancha)	2	на Гс2
T19	1	Плед на диван	1300×1700	альпака 50 %, шерсть 50 %			Tikkurila V484 (Driftwood)	1	на Гс2
T20**	4	Полотенца банные махровые, приглушённая олива, сложены на полотенцесушителе	700×1400	махра; хлопок 100 %; 550 г/м²			NCS S 5010-G70Y (приглушённая олива)	2	на Сн5; уход: 40 °C, без кондиционера
T21**	4	Полотенца для рук вафельные, тёплый белый, на нижних перекладинах сушителя	500×900	вафельное полотно; хлопок 100 %; 280 г/м²			Tikkurila F485 (Damask)	2	на Сн5; уход: 60 °C
T22**	4	Коврик для ванной у бортика ванны, хлопок тафтинг, песочный	800×450	хлопок 100 %, латексная противоскользящая основа			NCS S 2005-Y30R (песочный грейж)	1	противоскользящая подложка; ворс 12 мм; уход: 40 °C

образец цвета — по HEX производителя краски, справочно

Итого: шторы и тюль — 9 шт.; ковры и дорожки — 4 шт.; подушки, пледы, покрывала — 19 шт.


Образцы по помещениям

1. Гостиная-кухня

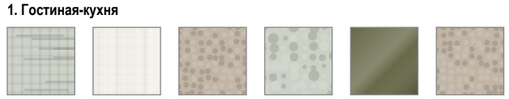


T13 T14 T16 T17 T18 T19

2. Спальня

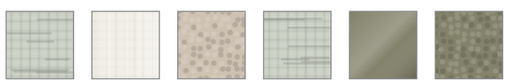

T1 T2 T3 T4 T5 T6

3. Детская

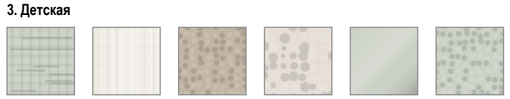

T7 T8 T9 T10 T11 T12

4. Санузел



T20** T21** T22**

Примечания

1. Коды цвета — ориентир подбора по веерам производителей красок; ткань утверждается по образцу при дневном свете и при свете проекта 2700–3000 K.
2. Размеры полотен — по замеру после чистовой отделки пола и потолка; ширина полотна указана с учётом сборки, без припусков на швы. Схемы окон и отметки шин лист 66.
3. Портьеры и тюль — на тесьме «волна» по системе шины; блэкаут — подкладкой. Ковры — на противоскользящей подложке.
4. Замена изделия — аналогом по характеристикам (состав, плотность, размер, цвет по образцу) с согласованием автора проекта.
5. Места изделий — план текстиля и декора (лист 65); подушки и пледы — по марке мебели.

Допущения и предложения на листе. Основа листа: размеры помещений и положение проёмов введены заказчиком в брифе, на объекте не замерены (К-1); высота потолка 2700 мм — по брифу заказчика, не замерена (К-2); толщины стен приняты по брифу: наружные 200 мм, внутренние 150 мм — не обмерены (К-1); тип дома монолитный, перекрытие 200 мм — по брифу заказчика, документов нет (К-3); планировка (стены, проёмы, объединение кухни и гостиной, расширение санузла) — по брифу без обмера и плана БТИ (К-7); разрешённая мощность 10 кВт принята, ТУ не переданы (К-8); вентканалы приняты, в брифе не заданы (К-9); подрайон климата не задан — принят не северный (жилые от 2,5 м) (К-10). Знак «**» — предложение проектировщика, заказчиком не утверждено (согласовать с заказчиком). См. лист открытых вопросов (лист 6, записи К-1–К-3, К-7–К-10; лист 7, запись ИЗ-3); по листу — ИЗ-3.

Изм.	Кол.уч	Лист	№ док.	Подп.	Дата
Разраб.		Кырлан А.С.			13.11.26
Пров.					
ГИП					
Н. контр.					
Утв.					

ГД-2026-011-АИ

Квартира 56 м²

ЖК «Северный парк», Москва

Дизайн-проект интерьера

Стадия	Лист	Листов
РП	67	119

Ведомость текстиля

М б/м

Кырлан Александр Сергеевич

выпуск 13.11.2026 № eb7810814f · стр. 75 из 139

Ведомость декора. Схемы развески

Картины, зеркала, растения, настольный декор · схемы развески (М 1:50) · высоты — мм от чистого пола


ПРЕДВАРИТЕЛЬНО · не для производства работ · открыто пунктов: 13 (реестр — л. 6, 7)

Декор: картины, зеркала, растения, предметы


картина · зеркало · мебель под изделием

Поз.	Пом.	Предмет	Размер, мм	Место: стена, высота от пола, мм	Масса, кг	Крепёж и основание	Свет места, отделка	Кол.
ДК1	2	Картина над кроватью: Ветка цветущей сакуры, акварель на тёплой бумаге	1000×700	стена Г, привязка 1300; низ 1100, центр 1450; над Сп1	4	подвес по основанию, 2 точки	рама — дуб	1
ДК2	4	Зеркало над умывальником, влагостойкое, с подсветкой	600×800	стена А, привязка 200; низ 1200, центр 1600; над Сн3		подвес по основанию, 2 точки		1
ДК3	3	Картина над кроватью: Серый кот спит на подоконнике у окна с бумажной ширмой, детская иллюстрация, гуашь	1200×600	стена Г, привязка 925; низ 900, центр 1200; над Дт1	4	подвес по основанию, 2 точки	рама — дуб	1
ДК4	3	Зеркало в рост в тонкой чёрной раме	500×1500	стена Б, привязка 1625; низ 300, центр 1050	12	анкер для пустотелых оснований, 4 шт.; основание: перегородка — определить обмером до монтажа; нагрузка 30 кг	рама — чёрный матовый металл	1
ДК5	5	Зеркало над скамьёй, тонкая чёрная рама	600×1200	стена В, привязка 2425; низ 700, центр 1300	18	анкер, 4 шт.; основание: перегородка — определить обмером до монтажа; нагрузка 40 кг	рама — чёрный матовый металл	1
ДК6	1	Картина над консолью: Горный ручей среди камней в тумане, тушь суми-э на бумаге васи	1000×700	стена В, привязка 2000; центр 1300; над Гс5**	6	анкер, 2 шт.; основание: перегородка — определить обмером до монтажа; нагрузка 15 кг		1
ДК7	1	Фикус каучуконосный в кашпо Ø450, глина	450×450	напольное			свет средний	1
ДК8	1	Ваза керамическая с одной веткой на обеденном столе	200×350	на Кх11 (обеденный стол)				1
ДК9**	4	Ваза-бутыль керамическая, приглушённая олива, с сухой веткой эвкалипта — на полке короба инсталляции	130×400	напольное			NCS S 5010-G70Y (приглушённая олива)	1
ДК10**	5	Графика в раме из тёмного ясеня 400×560: Энсо круг одним движением кисти, тушь	400×560	стена Г, привязка 65; низ 1220, центр 1500	2	дюбель с крюком, 2 точки; основание: перегородка — определить обмером до монтажа; нагрузка 10 кг	рама — тёмный ясень	1
ДК16**	2	Шеффлера в глиняном кашпо Ø350	380×380	напольное			свет средний	1


ДК1 — Спальня (пом. 2), стена Г (М 1:50)

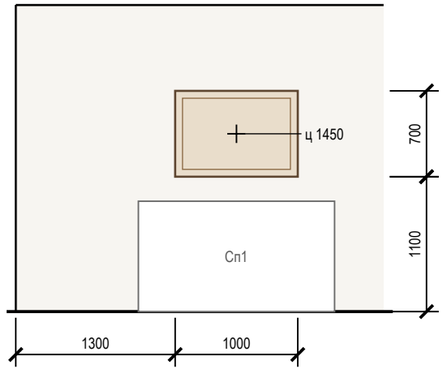


ДК2 — Санузел (пом. 4), стена А (М 1:50)

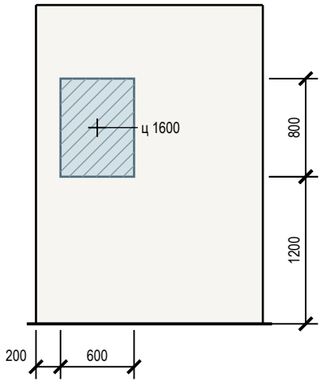

ДК3 — Детская (пом. 3), стена Г (М 1:50)

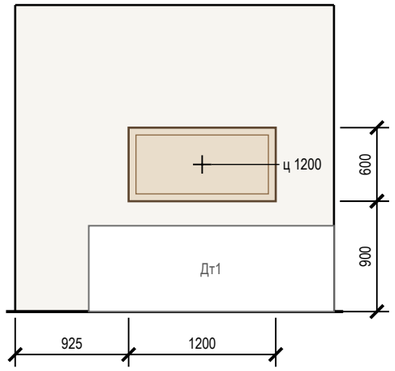

ДК4 — Детская (пом. 3), стена Б (М 1:50)

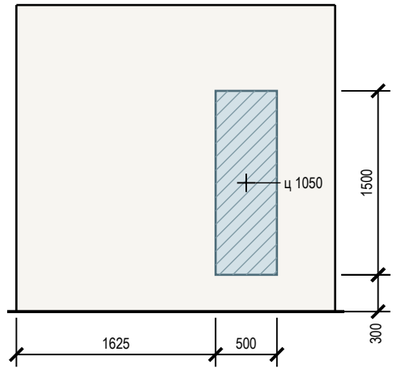

Допущения и предложения на листе

Основа листа: размеры помещений и положение проёмов введены заказчиком в брифе, на объекте не замерены (К-1); высота потолка 2700 мм — по брифу заказчика, не замерена (К-2); толщины стен приняты по брифу: наружные 200 мм, внутренние 150 мм — не обмерены (К-1); тип дома монолитный, перекрытие 200 мм — по брифу заказчика, документов нет (К-3); планировка (стены, проёмы, объединение кухни и гостиной, расширение санузла) — по брифу без обмера и плана БТИ (К-7); разрешённая мощность 10 кВт принята, ТУ не переданы (К-8); вентканалы приняты, в брифе не заданы (К-9); подрайон климата не задан — принят не северный (жилые от 2,5 м) (К-10).

Знак «**» — предложение проектировщика, заказчиком не утверждено (согласовать с заказчиком): ИЗ-1, ИЗ-3: Гс5 — Было смещение 1600…3400 у двери Д-2 (3700…4600): между консолью и креслом/диваном оставался проход 575–625 мм, из двери к кухне не пройти; ИЗ-3: ДК16, ДК9, ДК10.

Изменения по листу без подписи: ИЗ-3.

См. лист открытых вопросов (лист 6, записи К-1–К-3, К-7–К-10; лист 7, записи ИЗ-1, ИЗ-3).

Примечания

1. Высоты — от чистого пола помещения до низа изделия, «ц» — до центра; привязки — от чистовой грани угла стены, мм.
2. Над мебелью низ изделия — на 150–250 мм выше спинки или изголовья; без мебели центр — на 1450–1600 мм от пола.
3. Изделия до 5 кг — на два подвеса по основанию; тяжелее — на анкеры с нагрузкой не меньше двойной массы; на ГКЛ — только по закладной или анкеру для пустотелых оснований.
4. Зеркала в рост — с креплением от опрокидывания; в санузлах — влагостойкие, на клей для зеркал и нейтральный силикон.
5. Места изделий — план текстиля и декора (лист 65). Схемы развески остальных изделий — лист 69.

Изм.	Кол.уч	Лист	№ док.	Подп.	Дата
Разраб.		Кырлан А.С.			13.11.26
Пров.					
ГИП					
Н. контр.					
Утв.					

ГД-2026-011-АИ

Квартира 56 м²

ЖК «Северный парк», Москва

Дизайн-проект интерьера

Стадия	Лист	Листов
РП	68	119

Ведомость декора. Схемы развески

М б/м

Кырлан Александр Сергеевич

выпуск 13.11.2026 № eb7810814f · стр. 76 из 139


Схемы развески (продолжение)

Схемы развески картин и зеркал (М 1:40) · высоты — мм от чистого пола


Ведомость декора (размер, масса, крепёж и основание) — лист 68

картина · зеркало · мебель под изделием


ДК5 — Прихожая (пом. 5), стена В (М 1:40)

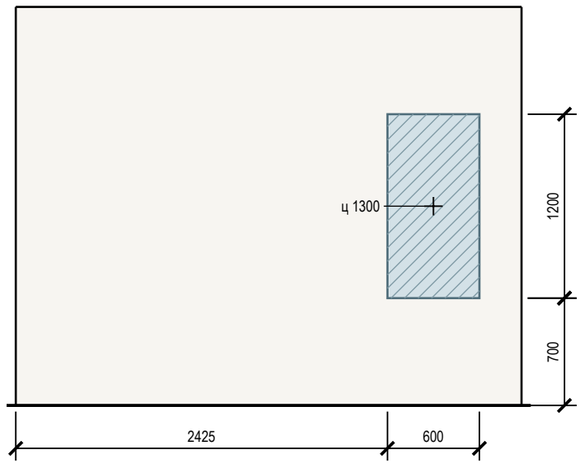

ДК6 — Гостиная-кухня (пом. 1), стена В (М 1:40)

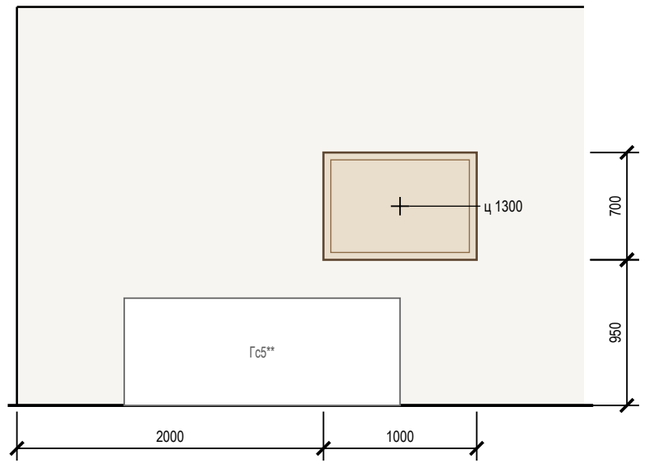

ДК10 — Прихожая (пом. 5), стена Г (М 1:40)**

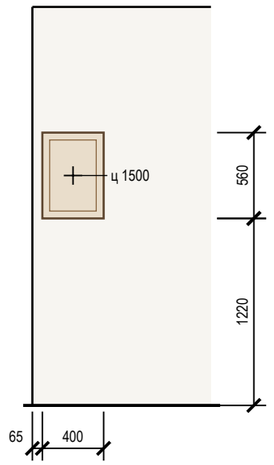

Допущения и предложения на листе

Основа листа: размеры помещений и положение проёмов введены заказчиком в брифе, на объекте не замерены (К-1); высота потолка 2700 мм — по брифу заказчика, не замерена (К-2); толщины стен приняты по брифу: наружные 200 мм, внутренние 150 мм — не обмерены (К-1); тип дома монолитный, перекрытие 200 мм — по брифу заказчика, документов нет (К-3); планировка (стены, проёмы, объединение кухни и гостиной, расширение санузла) — по брифу без обмера и плана БТИ (К-7); разрешённая мощность 10 кВт принята, ТУ не переданы (К-8); вентканалы приняты, в брифе не заданы (К-9); подрайон климата не задан — принят не северный (жилые от 2,5 м) (К-10).

Знак «**» — предложение проектировщика, заказчиком не утверждено (согласовать с заказчиком): ИЗ-1, ИЗ-3: Гс5 — Было смещение 1600…3400 у двери Д-2 (3700…4600): между консолью и креслом/диваном оставался проход 575–625 мм, из двери к кухне не пройти; ИЗ-3: ДК10.

См. лист открытых вопросов (лист 6, записи К-1–К-3, К-7–К-10; лист 7, записи ИЗ-1, ИЗ-3).

Примечания

1. Высоты — от чистого пола помещения до низа изделия, «ц» — до центра; привязки — от чистовой грани угла стены, мм.
2. Над мебелью низ изделия — на 150–250 мм выше спинки или изголовья; без мебели центр — на 1450–1600 мм от пола.
3. Изделия до 5 кг — на два подвеса по основанию; тяжелее — на анкеры с нагрузкой не меньше двойной массы; на ГКЛ — только по закладной или анкеру для пустотелых оснований.
4. Зеркала в рост — с креплением от опрокидывания; в санузлах — влагостойкие, на клей для зеркал и нейтральный силикон.
5. Места изделий — план текстиля и декора (лист 65). Ведомость декора: размер, масса, крепёж и основание — лист 68.

Изм.	Кол.уч	Лист	№ док.	Подп.	Дата
Разраб.		Кырлан А.С.			13.11.26
Пров.					
ГИП					
Н. контр.					
Утв.					

ГД-2026-011-АИ

Квартира 56 м²

ЖК «Северный парк», Москва

Дизайн-проект интерьера

Стадия	Лист	Листов
РП	69	119

Схемы развески (продолжение)

М б/м


Кырлан Александр Сергеевич

выпуск 13.11.2026 № eb7810814f · стр. 77 из 139

Встроенная мебель. Схема расположения

встроенная и корпусная мебель на заказ, кухонный гарнитур · размеры в мм · марки — по ведомости изделий

ПРЕДВАРИТЕЛЬНО · не для производства работ · открыто пунктов: 13 (реестр — л. 6, 7)

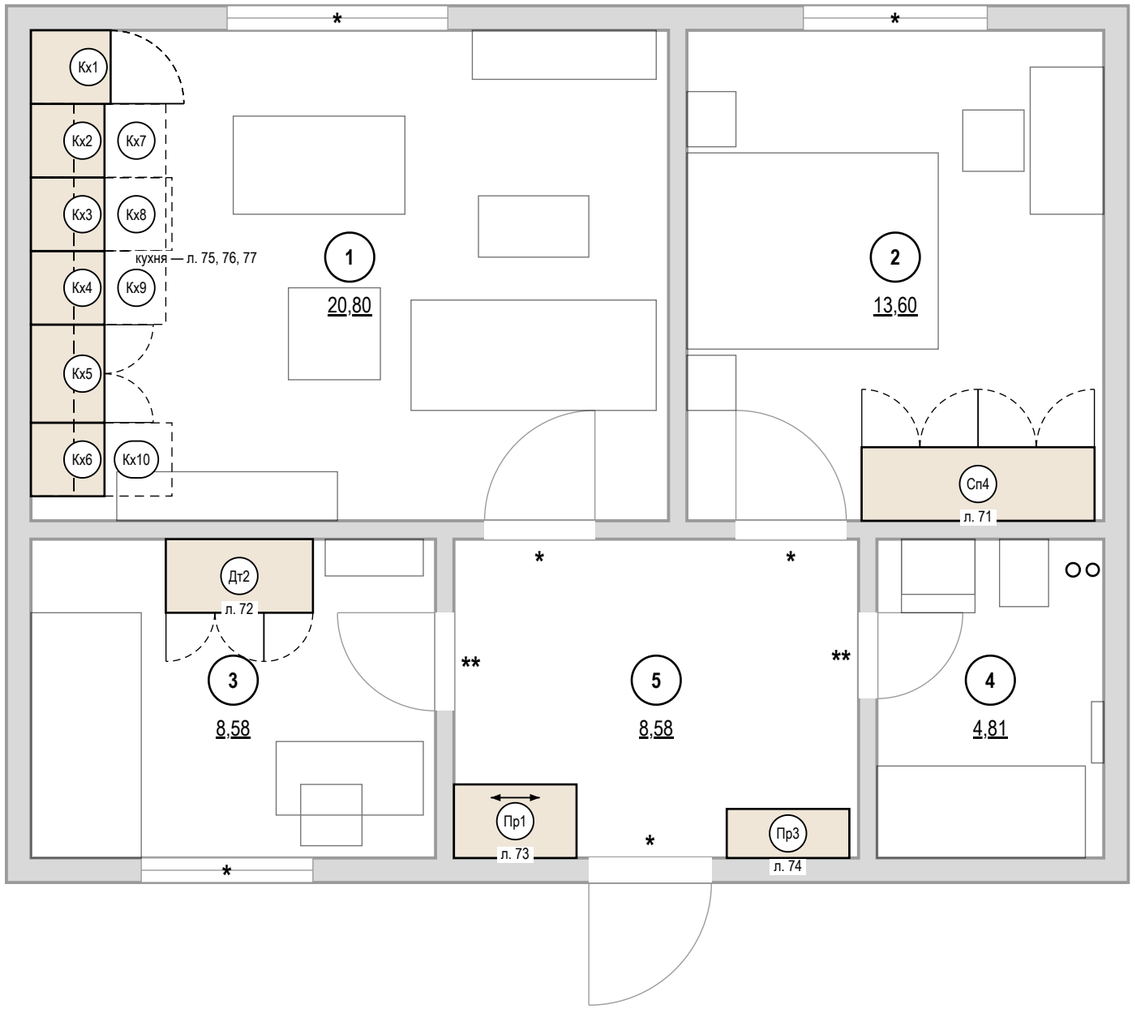

Ведомость изделий

Марка	Наименование	Пом.	Ш×Г×В, мм	Лист
Сп4	Шкаф распашной	2	1900×600×2400	71
Дт2	Шкаф распашной	3	1200×600×2200	72
Пр1	Шкаф-купе	5	1000×600×2510	73
Пр3	Система хранения	5	1000×400×500	74
Кх6	Модуль под ПММ 60: без корпуса, фасад на дверь машины	1	600×600×900	75, 76
Кх10	Модуль навесной: полки, сушка	1	1400×350×900	75, 76
Кх5	Модуль нижний: мойка	1	800×600×900	75, 76
Кх4	Модуль нижний: ящики	1	600×600×900	75, 76
Кх9	Модуль навесной: полки	1	600×350×900	75, 76
Кх3	Модуль нижний: духовой шкаф, варочная	1	600×600×900	75, 76
Кх8	Модуль навесной: полки	1	600×350×800	75, 76
Кх2	Модуль нижний: ящики	1	600×600×900	75, 76
Кх7	Модуль навесной: полки	1	600×350×900	75, 76
Кх1	Пенал: холодильник встр.	1	600×650×2350	75, 76

Условные обозначения

- изделие мебельщика: корпус на полу
- невидимый контур: навесной модуль, корпус под столешницей
- открывание распашного фасада
- зона выдвижения ящика, двери техники
- дверь купе, стрелка — направление движения
- К1 — марка изделия или модуля (на схеме расположения под ней — лист изделия)
- * — «*» — принято, не замерено и не подтверждено
- ** — «**» — предложение проектировщика, заказчиком не утверждено

Допущения и предложения на листе. Основа листа: размеры помещений и положение проёмов введены заказчиком в брифе, на объекте не замерены (К-1); высота потолка 2700 мм — по брифу заказчика, не замерена (К-2); толщины стен приняты по брифу: наружные 200 мм, внутренние 150 мм — не обмерены (К-1); тип дома монолитный, перекрытие 200 мм — по брифу заказчика, документов нет (К-3); планировка (стены, проёмы, объединение кухни и гостиной, расширение санузла) — по брифу без обмера и плана БТИ (К-7); разрешённая мощность 10 кВт принята, ТУ не переданы (К-8); вентканалы приняты, в брифе не заданы (К-9); подрайон климата не задан — принят не северный (жилые от 2,5 м) (К-10). Знак «*» — принято, не замерено и не подтверждено (замерить на объекте): К-4: Ст К1-1 — положение стояка канализации — по брифу заказчика, не замерено; Ст В1-1 — положение стояка холодной воды — по брифу заказчика, не замерено. Знак «**» — предложение проектировщика, заказчиком не утверждено (согласовать с заказчиком). См. лист открытых вопросов (лист 6, записи К-1–К-5, К-7–К-10).

Примечания

1. Изделия — по чистовым размерам помещений; перед раскроем — контрольный замер цеха после чистовой отделки стен, пола и потолка.
2. Открывание фасадов и выдвижение ящиков показано в открытом положении: зоны не пересекают двери, радиаторы, выключатели и проходы.
3. Стояки и счётчики за мебелью — с сервисным люком; газовые трубы мебелью не зашиваются.
4. Покупная мебель — по плану расстановки мебели и спецификации дизайнера; здесь — подложкой.
5. Знак «*» у проёма — положение не замерено; реестр: листы 6–7, вопросы К-1, К-11.

1000 мм · печать 1:1

Изм.	Кол.уч	Лист	№ док.	Подп.	Дата
Разраб.		Кырлан А.С.			13.11.26
Пров.					
ГИП					
Н. контр.					
Утв.					

ГД-2026-011-АИ

Квартира 56 м²

ЖК «Северный парк», Москва

Дизайн-проект интерьера

Стадия	Лист	Листов
РП	70	119

Встроенная мебель. Схема расположения

М 1:50

Кырлан Александр Сергеевич


выпуск 13.11.2026 № eb7810814f · стр. 78 из 139

Шкаф распашной Сп4


Спальня (пом. 2) · вид из помещения · размеры в мм, отметки в м

ПРЕДВАРИТЕЛЬНО · не для производства работ · открыто пунктов: 13 (реестр — л. 6, 7)


Вид с фасадами (М 1:20)

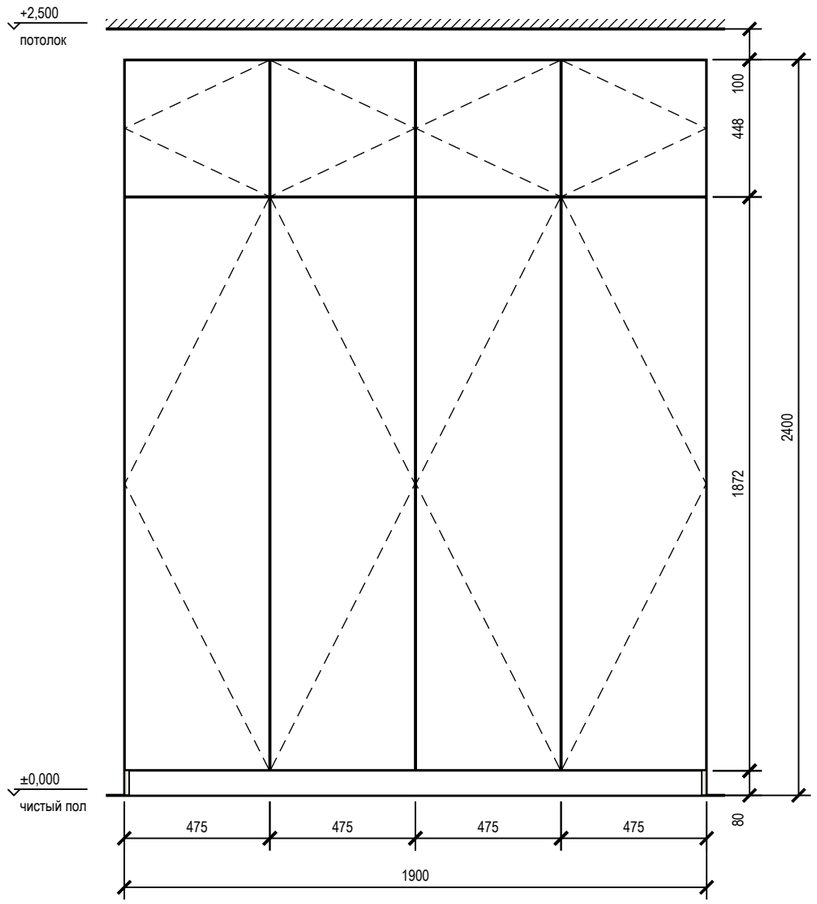


Вид без фасадов (М 1:20)

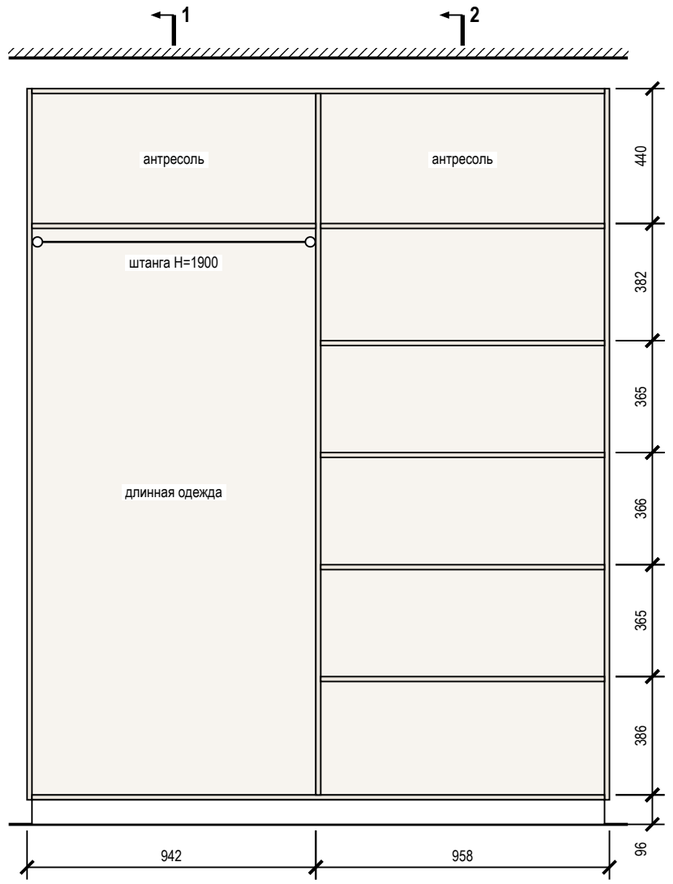

Разрез 1-1 (М 1:20)

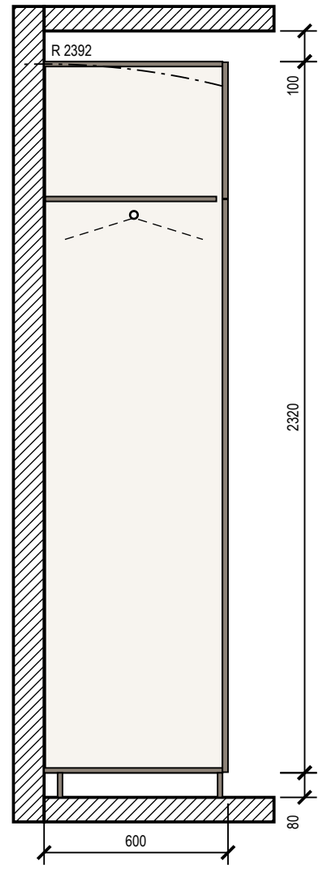

Разрез 2-2 (М 1:20)

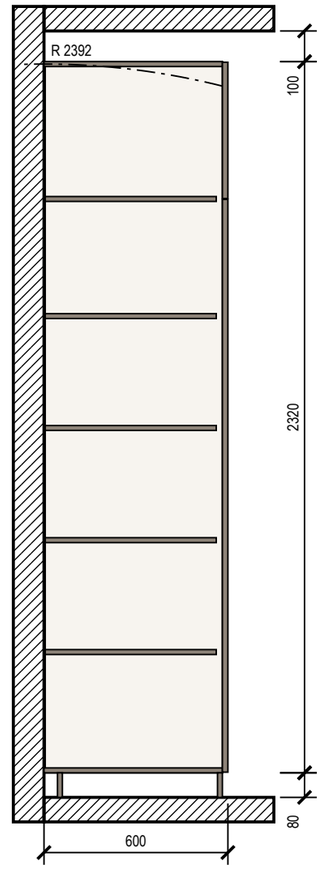

Примечания

1. Размеры — в мм по чистовой отделке; изделие 1900×600×2400 (Ш×Г×В). Перед раскроем — контрольный замер цеха после чистовой отделки стен, пола и потолка.
2. Корпус — ЛДСП 16 мм, задняя стенка ХДФ 4 мм в паз, цоколь 80 мм на регулируемых опорах; фасады накладные — МДФ 18 мм, эмаль матовая, 18 мм; цвет — по колерной карте; петли с доводчиком: фасад 1869 мм — 4 петли, фасад 445 мм — 2 петли.
3. Кромка: скрытые торцы 0,4 мм, видимые 2 мм (ПВХ/АБС).
4. Номинальные зазоры: между фасадами 3 мм, фасад — стена и фасад — потолок не менее 3 мм, фасад ящика — стойка 2 мм.
5. Присадка по 32-й системе — выполняет цех.
6. Зазор до потолка 100 мм — закрыть планкой в цвет корпуса при монтаже.
7. Подъём корпуса: диагональ боковины без цоколя √(2320² + 582²) = 2392 мм < 2500 мм до потолка — корпус собирается лёжа, поднимается поворотом и ставится на цоколь.
8. Крепление к стене от опрокидывания: уголок к стене, 2 шт.; основание стены и шаг анкеров — монтажная схема шкафов.

Условные обозначения

- фасад распашной: линии сходятся к стороне петель
- корпус и полки ЛДСП (вид на стену)
- задняя стенка ХДФ
- деталь в разрезе
- штанга для плечиков (на разрезе — плечики 450 мм)
- траектория угла корпуса при подъёме в проектное положение

Допущения и предложения на листе

Основа листа: размеры помещений и положение проёмов введены заказчиком в брифе, на объекте не замерены (К-1); высота потолка 2700 мм — по брифу заказчика, не замерена (К-2); толщины стен приняты по брифу: наружные 200 мм, внутренние 150 мм — не обмерены (К-1); тип дома монолитный, перекрытие 200 мм — по брифу заказчика, документов нет (К-3); планировка (стены, проёмы, объединение кухни и гостиной, расширение санузла) — по брифу без обмера и плана БТИ (К-7); разрешённая мощность 10 кВт принята, ТУ не переданы (К-8); вентканалы приняты, в брифе не заданы (К-9); подрайон климата не задан — принят не северный (жилые от 2,5 м) (К-10).
См. лист открытых вопросов (лист 6, записи К-1–К-3, К-7–К-10).

1000 мм · печать 1:1

Изм.	Кол.уч	Лист	№ док.	Подп.	Дата
Разраб.		Кырлан А.С.			13.11.26
Пров.					
ГИП					
Н. контр.					
Утв.					

ГД-2026-011-АИ

Квартира 56 м²

ЖК «Северный парк», Москва

Дизайн-проект интерьера

Стадия	Лист	Листов
РП	71	119

Шкаф распашной Сп4

М 1:20

Кырлан Александр Сергеевич


выпуск 13.11.2026 № eb7810814f · стр. 79 из 139

Шкаф распашной Дт2


Детская (пом. 3) · вид из помещения · размеры в мм, отметки в м

ПРЕДВАРИТЕЛЬНО · не для производства работ · открыто пунктов: 13 (реестр — л. 6, 7)


Вид с фасадами (М 1:20)

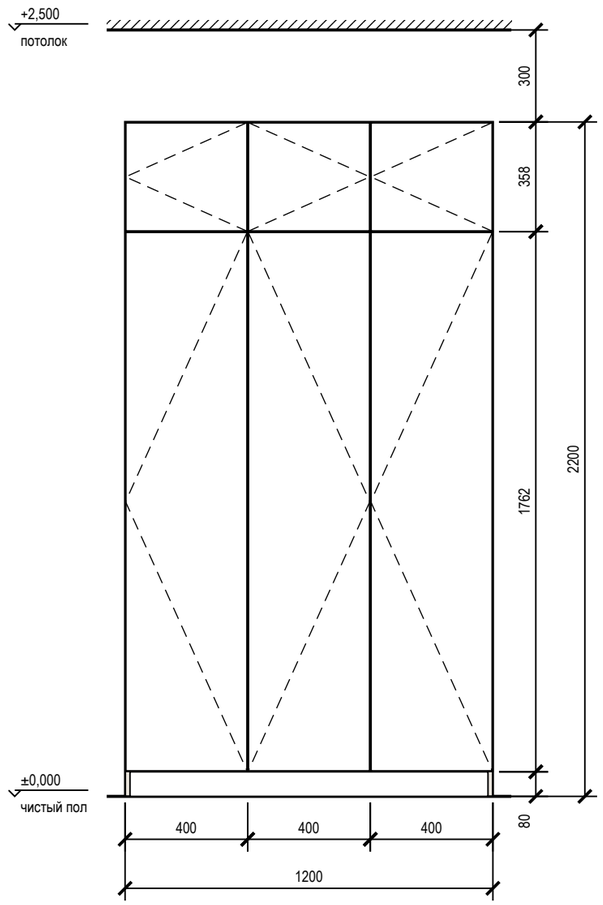


Вид без фасадов (М 1:20)

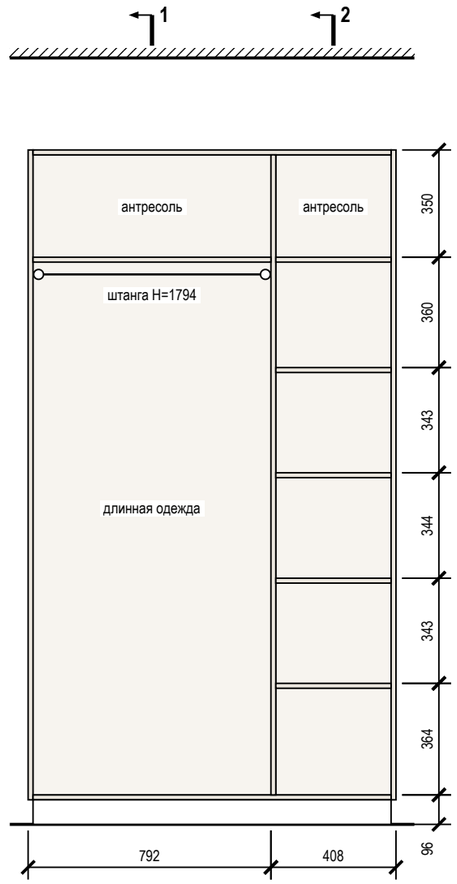

Разрез 1-1 (М 1:20)

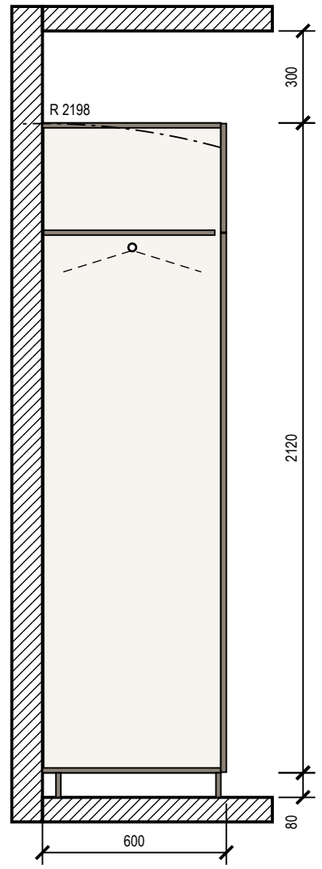

Разрез 2-2 (М 1:20)

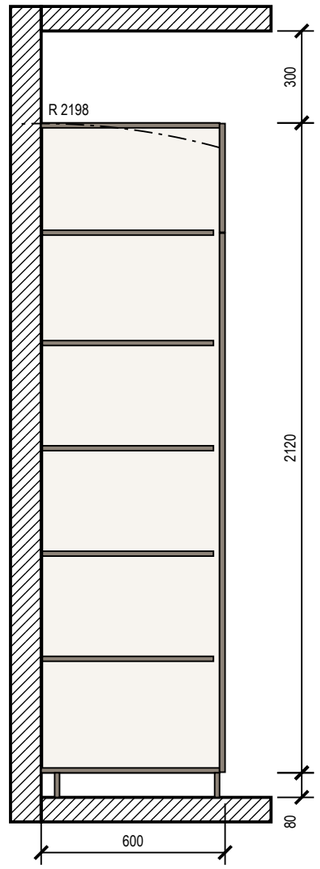

Примечания

1. Размеры — в мм по чистовой отделке; изделие 1200×600×2200 (Ш×Г×В). Перед раскроем — контрольный замер цеха после чистовой отделки стен, пола и потолка.
2. Корпус — ЛДСП 16 мм, задняя стенка ХДФ 4 мм в паз, цоколь 80 мм на регулируемых опорах; фасады накладные — МДФ 18 мм, эмаль матовая, 18 мм; цвет — по колерной карте; петли с доводчиком: фасад 1759 мм — 4 петли, фасад 355 мм — 2 петли.
3. Кромка: скрытые торцы 0,4 мм, видимые 2 мм (ПВХ/АБС).
4. Номинальные зазоры: между фасадами 3 мм, фасад — стена и фасад — потолок не менее 3 мм, фасад ящика — стойка 2 мм.
5. Присадка по 32-й системе — выполняет цех.
6. Зазор до потолка 300 мм.
7. Подъём корпуса: диагональ боковины без цоколя $\sqrt{(2120^2 + 582^2)} = 2198$ мм < 2500 мм до потолка — корпус собирается лёжа, поднимается поворотом и ставится на цоколь.
8. Крепление к стене от опрокидывания: уголок к стене, 2 шт.; основание стены и шаг анкеров — монтажная схема шкафов.

Условные обозначения

- фасад распашной: линии сходятся к стороне петель
- корпус и полки ЛДСП (вид на стену)
- задняя стенка ХДФ
- деталь в разрезе
- штанга для плечиков (на разрезе — плечики 450 мм)
- траектория угла корпуса при подъёме в проектное положение

Допущения и предложения на листе

Основа листа: размеры помещений и положение проёмов введены заказчиком в брифе, на объекте не замерены (К-1); высота потолка 2700 мм — по брифу заказчика, не замерена (К-2); толщины стен приняты по брифу: наружные 200 мм, внутренние 150 мм — не обмерены (К-1); тип дома монолитный, перекрытие 200 мм — по брифу заказчика, документов нет (К-3); планировка (стены, проёмы, объединение кухни и гостиной, расширение санузла) — по брифу без обмера и плана БТИ (К-7); разрешённая мощность 10 кВт принята, ТУ не переданы (К-8); вентканалы приняты, в брифе не заданы (К-9); подрайон климата не задан — принят не северный (жилые от 2,5 м) (К-10).
См. лист открытых вопросов (лист 6, записи К-1–К-3, К-7–К-10).

1000 мм · печать 1:1

Изм.	Кол.уч	Лист	№ док.	Подп.	Дата
Разраб.		Кырлан А.С.			13.11.26
Пров.					
ГИП					
Н. контр.					
Утв.					

ГД-2026-011-АИ

Квартира 56 м²

ЖК «Северный парк», Москва

Дизайн-проект интерьера

Стадия	Лист	Листов
РП	72	119

Шкаф распашной Дт2

М 1:20

Кырлан Александр Сергеевич


выпуск 13.11.2026 № eb7810814f · стр. 80 из 139

Шкаф-купе Пр1


Прихожая (пом. 5) · вид из помещения · размеры в мм, отметки в м

ПРЕДВАРИТЕЛЬНО · не для производства работ · открыто пунктов: 13 (реестр — л. 6, 7)


Вид с фасадами (М 1:20)

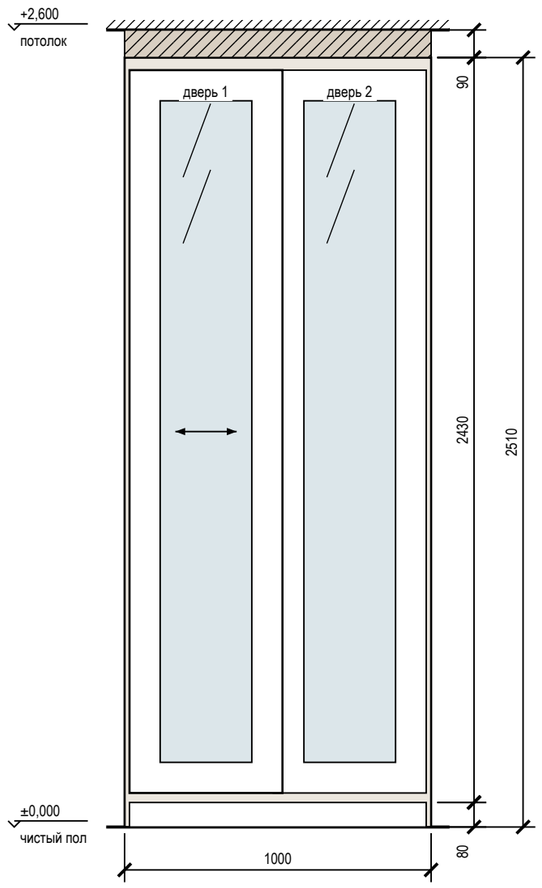


Вид без фасадов (М 1:20)

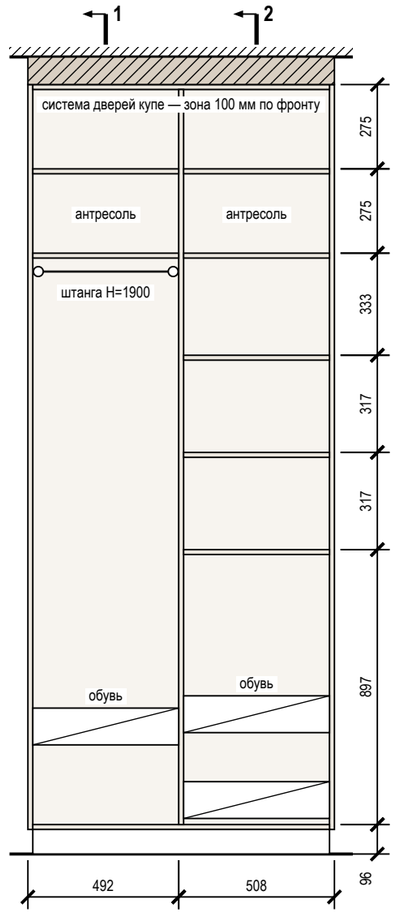

Разрез 1-1 (М 1:20)

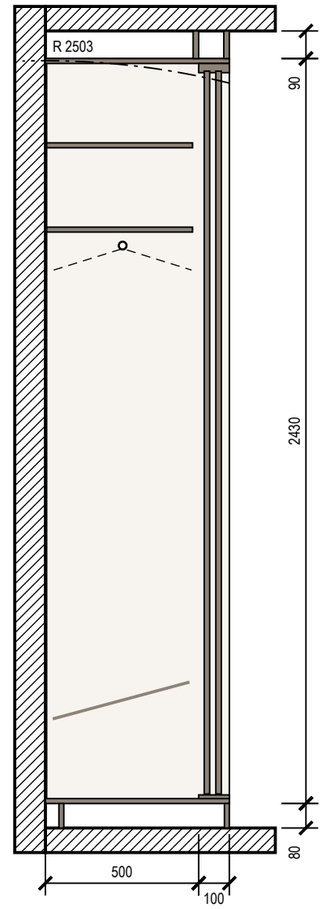

Разрез 2-2 (М 1:20)

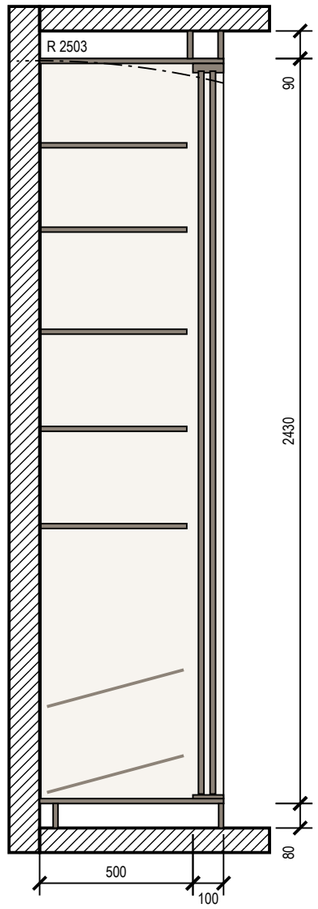

Примечания

1. Размеры — в мм по чистовой отделке; изделие 1000×600×2510 (Ш×Г×В). Перед раскроем — контрольный замер цеха после чистовой отделки стен, пола и потолка.
2. Корпус — ЛДСП 16 мм, задняя стенка ХДФ 4 мм в паз, цоколь 80 мм на регулируемых опорах; двери купе — ЛДСП 10 мм, декор «дуб натуральный» в профиле: алюминий, чёрный матовый; вставка — зеркало серебро 4 мм, плёнка безопасности; нахлёст 30 мм, ширина двери 499 мм, высота — проём минус 40 мм; цвет — по колерной карте.
3. Кромка: скрытые торцы 0,4 мм, видимые 2 мм (ПВХ/АБС).
4. Номинальные зазоры: дверь купе — боковина 3 мм, фасад ящика — стойка 2 мм; ящики внутри купе — с накладкой 30 мм на стойке со стороны нахлёста дверей.
5. Присадка по 32-й системе — выполняет цех.
6. Компенсатор 90 мм — короб из ЛДСП по фронту и торцам, подгоняется к потолку при монтаже (припуск 20 мм), крепится к корпусу и к потолку.
7. Подъём корпуса: диагональ боковины без цоколя √(2430² + 600²) = 2503 мм < 2600 мм до потолка — корпус собирается лёжа, поднимается поворотом и ставится на цоколь.
8. Крепление к стене от опрокидывания — уголки 2 шт. к несущему основанию (монтажная схема шкафов).

Условные обозначения

- дверь купе, стрелка — направление движения
- корпус и полки ЛДСП (вид на стену)
- задняя стенка ХДФ
- деталь в разрезе
- компенсатор — короб до потолка
- зеркальная вставка фасада
- штанга для плечиков (на разрезе — плечики 450 мм)
- траектория угла корпуса при подъёме в проектное положение

Допущения и предложения на листе

Основа листа: размеры помещений и положение проёмов введены заказчиком в брифе, на объекте не замерены (К-1); высота потолка 2700 мм — по брифу заказчика, не замерена (К-2); толщины стен приняты по брифу: наружные 200 мм, внутренние 150 мм — не обмерены (К-1); тип дома монолитный, перекрытие 200 мм — по брифу заказчика, документов нет (К-3); планировка (стены, проёмы, объединение кухни и гостиной, расширение санузла) — по брифу без обмера и плана БТИ (К-7); разрешённая мощность 10 кВт принята, ТУ не переданы (К-8); вентканалы приняты, в брифе не заданы (К-9); подрайон климата не задан — принят не северный (жилые от 2,5 м) (К-10).
См. лист открытых вопросов (лист 6, записи К-1–К-3, К-7–К-10).

1000 мм · печать 1:1

Изм.	Кол.уч	Лист	№ док.	Подп.	Дата
Разраб.		Кырлан А.С.			13.11.26
Пров.					
ГИП					
Н. контр.					
Утв.					

ГД-2026-011-АИ

Квартира 56 м²

ЖК «Северный парк», Москва

Дизайн-проект интерьера

Стадия	Лист	Листов
РП	73	119

Шкаф-купе Пр1

М 1:20

Кырлан Александр Сергеевич


выпуск 13.11.2026 № eb78108l4f · стр. 81 из 139

Система хранения Пр3


Прихожая (пом. 5) · вид из помещения · размеры в мм, отметки в м

ПРЕДВАРИТЕЛЬНО · не для производства работ · открыто пунктов: 13 (реестр — л. 6, 7)


Общий вид (М 1:20)

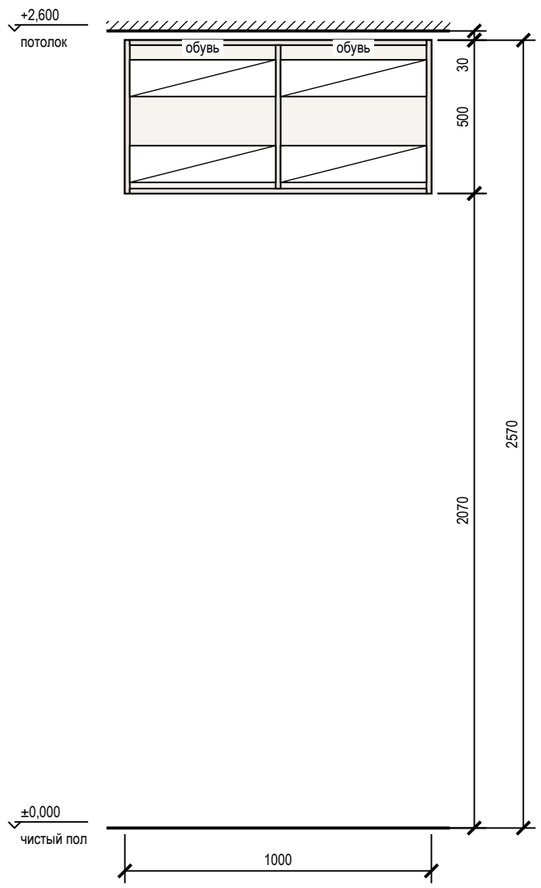

Наполнение, размеры в свету (М 1:20)

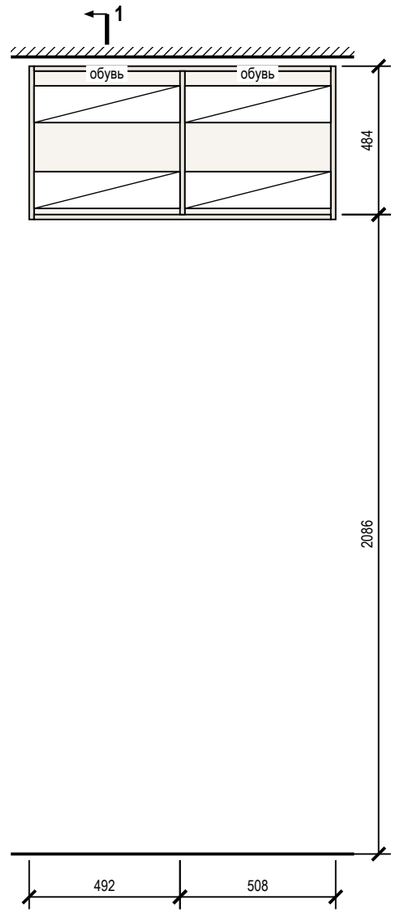

Разрез 1-1 (М 1:20)

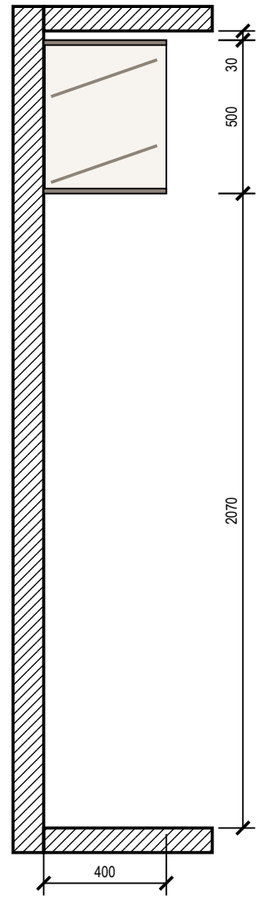

Примечания

1. Размеры — в мм по чистовой отделке; изделие 1000×400×500 (Ш×Г×В). Перед раскроем — контрольный замер цеха после чистовой отделки стен, пола и потолка.
2. Корпус — ЛДСП 16 мм, задняя стенка ХДФ 4 мм в паз, навесной корпус без цоколя, низ на 2070 мм от чистого пола; открытая система: без фасадов.
3. Кромка: скрытые торцы 0,4 мм, видимые 2 мм (ПВХ/АБС).
4. Присадка по 32-й системе — выполняет цех.
5. Зазор до потолка 30 мм — закрыть планкой в цвет корпуса при монтаже.
6. Навесной корпус — на стене: регулируемые навесы на монтажную шину или анкеры в несущее основание; основание стены и шаг анкеров — монтажная схема шкафов.

Условные обозначения

- корпус и полки ЛДСП (вид на стену)
- задняя стенка ХДФ
- деталь в разрезе
- штанга для плечиков (на разрезе — плечики 450 мм)

Допущения и предложения на листе

Основа листа: размеры помещений и положение проёмов введены заказчиком в брифе, на объекте не замерены (К-1); высота потолка 2700 мм — по брифу заказчика, не замерена (К-2); толщины стен приняты по брифу: наружные 200 мм, внутренние 150 мм — не обмерены (К-1); тип дома монолитный, перекрытие 200 мм — по брифу заказчика, документов нет (К-3); планировка (стены, проёмы, объединение кухни и гостиной, расширение санузла) — по брифу без обмера и плана БТИ (К-7); разрешённая мощность 10 кВт принята, ТУ не переданы (К-8); вентканалы приняты, в брифе не заданы (К-9); подрайон климата не задан — принят не северный (жилые от 2,5 м) (К-10).

См. лист открытых вопросов (лист 6, записи К-1–К-3, К-7–К-10).

1000 мм · печать 1:1

Изм.	Кол.уч	Лист	№ док.	Подп.	Дата
Разраб.		Кырлан А.С.			13.11.26
Пров.					
ГИП					
Н. контр.					
Утв.					

ГД-2026-011-АИ

Квартира 56 м²

ЖК «Северный парк», Москва

Дизайн-проект интерьера

Стадия	Лист	Листов
РП	74	119

Система хранения Пр3

М 1:20

Кырлан Александр Сергеевич


выпуск 13.11.2026 № eb78108814f · стр. 82 из 139

Кухня (пом. 1). Развёртка гарнитура

Гостиная-кухня (пом. 1) · стена Г · вид из помещения · размеры в мм, отметки в м · лист 1: вид с фасадами

ПРЕДВАРИТЕЛЬНО · не для производства работ · открыто пунктов: 13 (реестр — л. 6, 7)

Вид с фасадами (М 1:20)

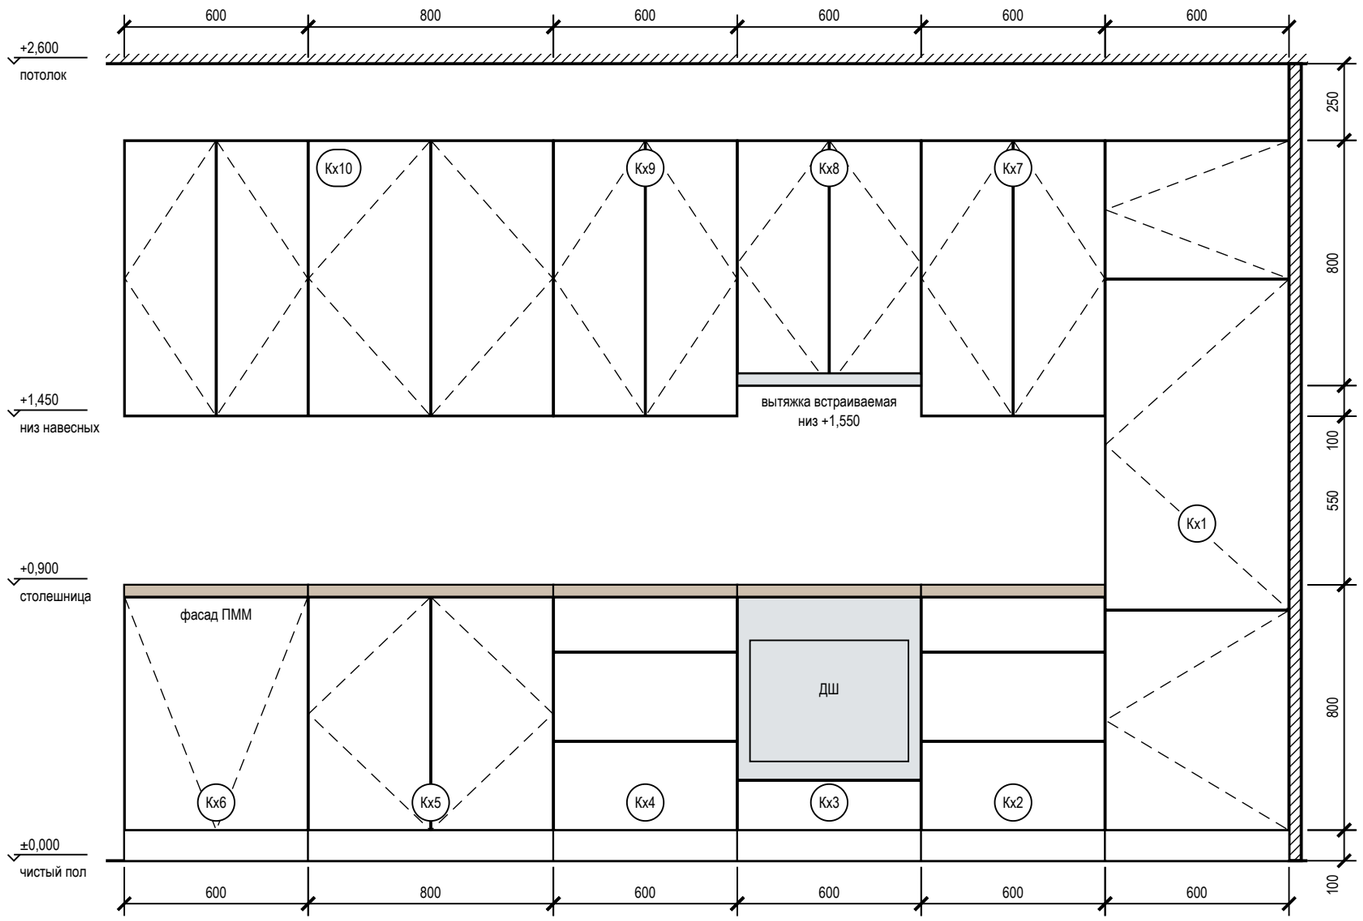

Условные обозначения

- фасад распашной: линии сходятся к стороне петель
- фасад ящика, карго
- встраиваемая техника
- столешница
- доборная планка
- деталь в разрезе
- К1 — марка изделия или модуля (на схеме расположения под ней — лист изделия)
- розетка на стене
- вывод кабеля к технике
- В1 — вывод воды В1 / Т3, канализации К1

Примечания

1. Размеры — в мм по чистовой отделке, вид из помещения; марки — как на плане расстановки. Перед раскроем контрольный замер цеха после фартука и пола.
2. Корпуса — ЛДСП 16 мм, задняя стенка ХДФ 4 мм; фасады — МДФ, эмаль матовая 18 мм, цвет по колерной карте; столешница 38 мм, свес 20 мм; цоколь 100 мм.
3. Кромка: скрытые торцы 0,4 мм, видимые 2 мм. Номинальные зазоры: между фасадами 3 мм, фасад — столешница 3 мм, фасад — стена не менее 3 мм.
4. Ящики полного выдвижения и петли — с доводчиком; присадка по 32-й системе — выполняет цех.

Ведомость модулей

Мод.	Наименование	Ш×Г×В, мм	Низ, мм
Кх6	Модуль под ПММ 60: без корпуса, фасад на дверь машины	600×600×900	от цоколя
Кх5	Модуль нижний: мойка	800×600×900	от цоколя
Кх4	Модуль нижний: ящики	600×600×900	от цоколя
Кх3	Модуль нижний: духовой шкаф, варочная	600×600×900	от цоколя
Кх2	Модуль нижний: ящики	600×600×900	от цоколя

Мод.	Наименование	Ш×Г×В, мм	Низ, мм
Кх10	Модуль навесной: полки, сушка	1400×350×900	+1450
Кх9	Модуль навесной: полки	600×350×900	+1450
Кх8	Модуль навесной: полки	600×350×800	+1550
Кх7	Модуль навесной: полки	600×350×900	+1450
Кх1	Пенал: холодильник встр.	600×650×2350	от пола

Допущения и предложения на листе

Основа листа: размеры помещений и положение проёмов введены заказчиком в брифе, на объекте не замерены (К-1); высота потолка 2700 мм — по брифу заказчика, не замерена (К-2); толщины стен приняты по брифу: наружные 200 мм, внутренние 150 мм — не обмерены (К-1); тип дома монолитный, перекрытие 200 мм — по брифу заказчика, документов нет (К-3); планировка (стены, проёмы, объединение кухни и гостиной, расширение санузла) — по брифу без обмера и плана БТИ (К-7); разрешённая мощность 10 кВт принята, ТУ не переданы (К-8); вентканалы приняты, в брифе не заданы (К-9); подрайон климата не задан — принят не северный (жилые от 2,5 м) (К-10).

См. лист открытых вопросов (лист 6, записи К-1–К-3, К-7–К-10).

1000 мм · печать 1:1

Изм.	Кол.уч	Лист	№ док.	Подп.	Дата
Разраб.		Кырлан А.С.			13.11.26
Пров.					
ГИП					
Н. контр.					
Утв.					

ГД-2026-011-АИ

Квартира 56 м²

ЖК «Северный парк», Москва

Дизайн-проект интерьера

Стадия	Лист	Листов
РП	75	119

Кухня (пом. 1). Развёртка гарнитура

М 1:20

Кырлан Александр Сергеевич


выпуск 13.11.2026 № eb7810814f · стр. 83 из 139

Кухня (пом. 1). Развёртка гарнитура: вид без фасадов и разрезы


ПРЕДВАРИТЕЛЬНО · не для производства работ · открыто пунктов: 13 (реестр — л. 6, 7)

Гостиная-кухня (пом. 1) · стена Г · вид из помещения · размеры в мм, отметки в м · лист 2: вид без фасадов, разрезы


Вид без фасадов: наполнение, выводы (М 1:20)

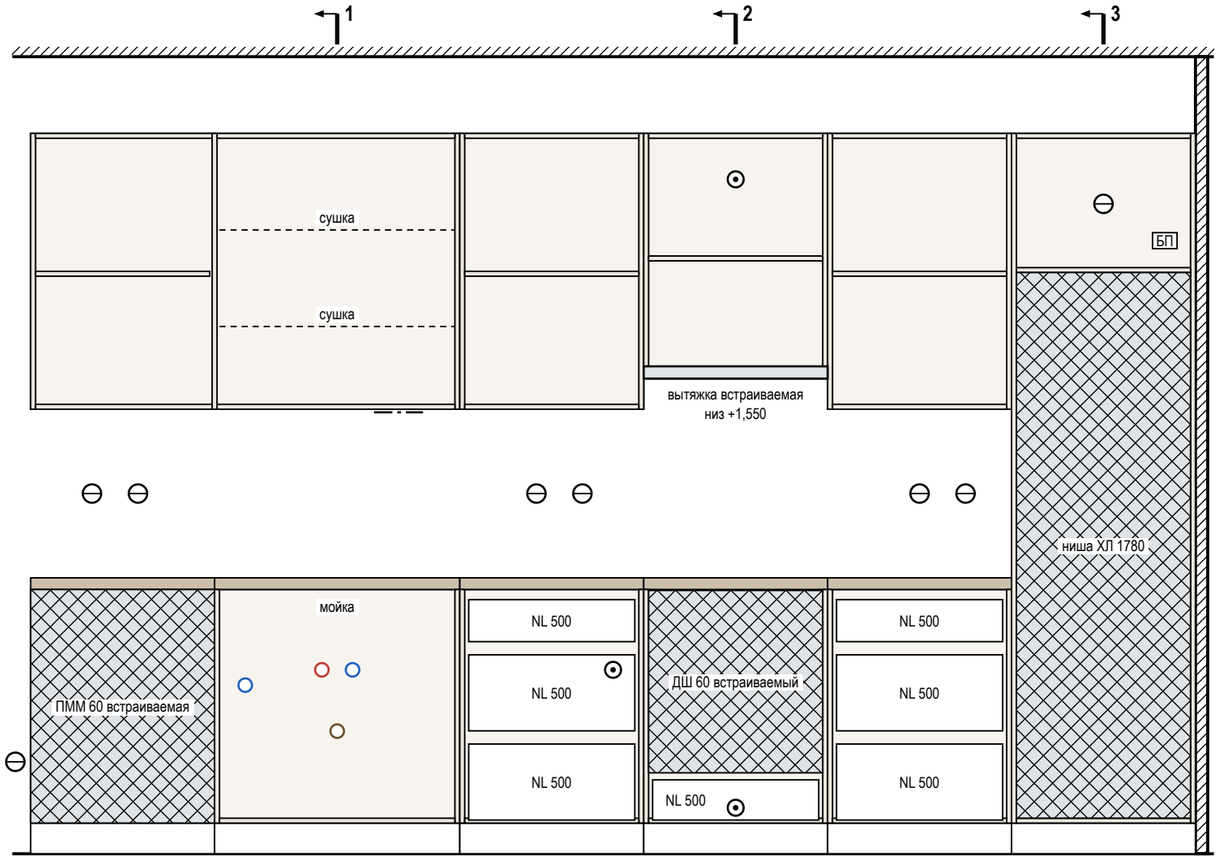


Разрез 1-1 (М 1:20)

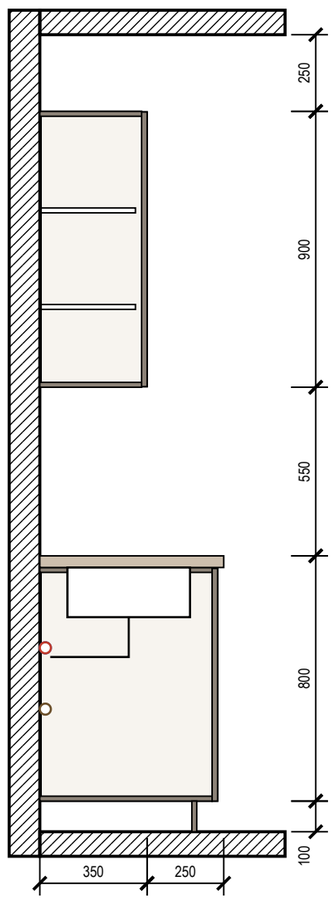

Разрез 2-2 (М 1:20)

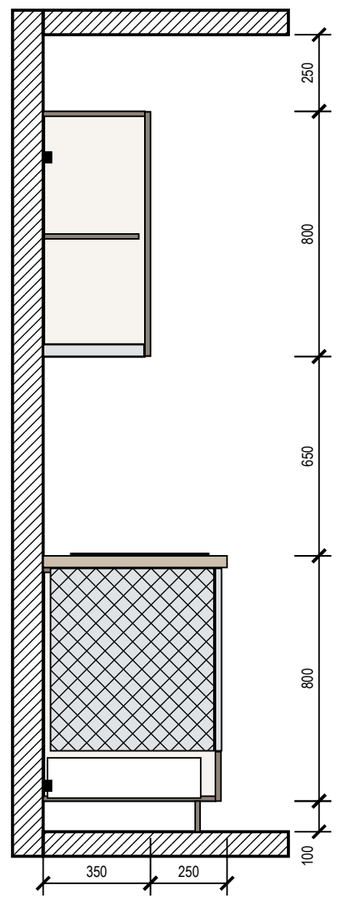

Разрез 3-3 (М 1:20)

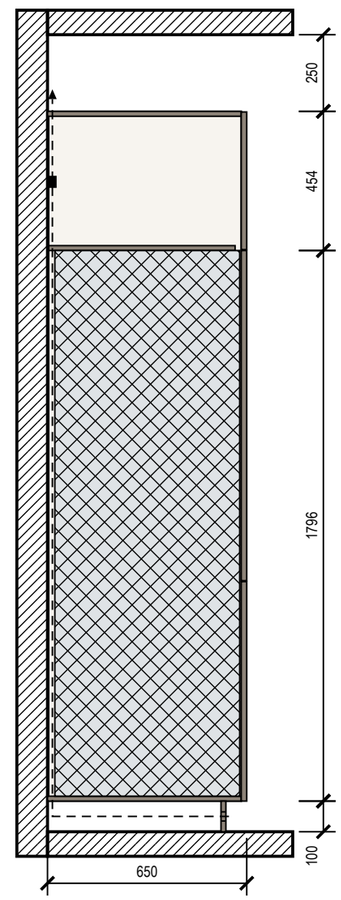

Примечания

1. Вытяжка встраивается в дно навесного модуля Кх8 над варочной: её низ на 1550 мм от пола, 650 мм над панелью (не меньше 650 мм).
2. Ниши техники (холодильник — ориентир 1780 мм) — по монтажным схемам выбранных моделей: решётка в цоколе и канал за пеналом холодильника, зазор за духовым шкафом, фасад ПММ на двери машины.

Допущения и предложения на листе

Основа листа: размеры помещений и положение проёмов введены заказчиком в брифе, на объекте не замерены (К-1); высота потолка 2700 мм — по брифу заказчика, не замерена (К-2); толщины стен приняты по брифу: наружные 200 мм, внутренние 150 мм — не обмерены (К-1); тип дома монолитный, перекрытие 200 мм — по брифу заказчика, документов нет (К-3); планировка (стены, проёмы, объединение кухни и гостиной, расширение санузла) — по брифу без обмера и плана БТИ (К-7); разрешённая мощность 10 кВт принята, ТУ не переданы (К-8); вентканалы приняты, в брифе не заданы (К-9); подрайон климата не задан — принят не северный (жилые от 2,5 м) (К-10).
См. лист открытых вопросов (лист 6, записи К-1–К-3, К-7–К-10).

1000 мм · печать 1:1

Изм.	Кол.уч	Лист	№ док.	Подп.	Дата
Разраб.		Кырлан А.С.			13.11.26
Пров.					
ГИП					
Н. контр.					
Утв.					

ГД-2026-011-АИ

Квартира 56 м²

ЖК «Северный парк», Москва

Дизайн-проект интерьера

Стадия	Лист	Листов
РП	76	119

Кухня (пом. 1). Развёртка гарнитура: вид без фасадов и разрезы

М 1:20


Кырлан Александр Сергеевич

Кухня (пом. 1). Монтажная схема


Гостиная-кухня (пом. 1) · стена Г · размеры в мм от чистых поверхностей, высоты — от чистого пола

ПРЕДВАРИТЕЛЬНО · не для производства работ · открыто пунктов: 13 (реестр — л. 6, 7)

Привязка выводов и крепление модулей (М 1:25)

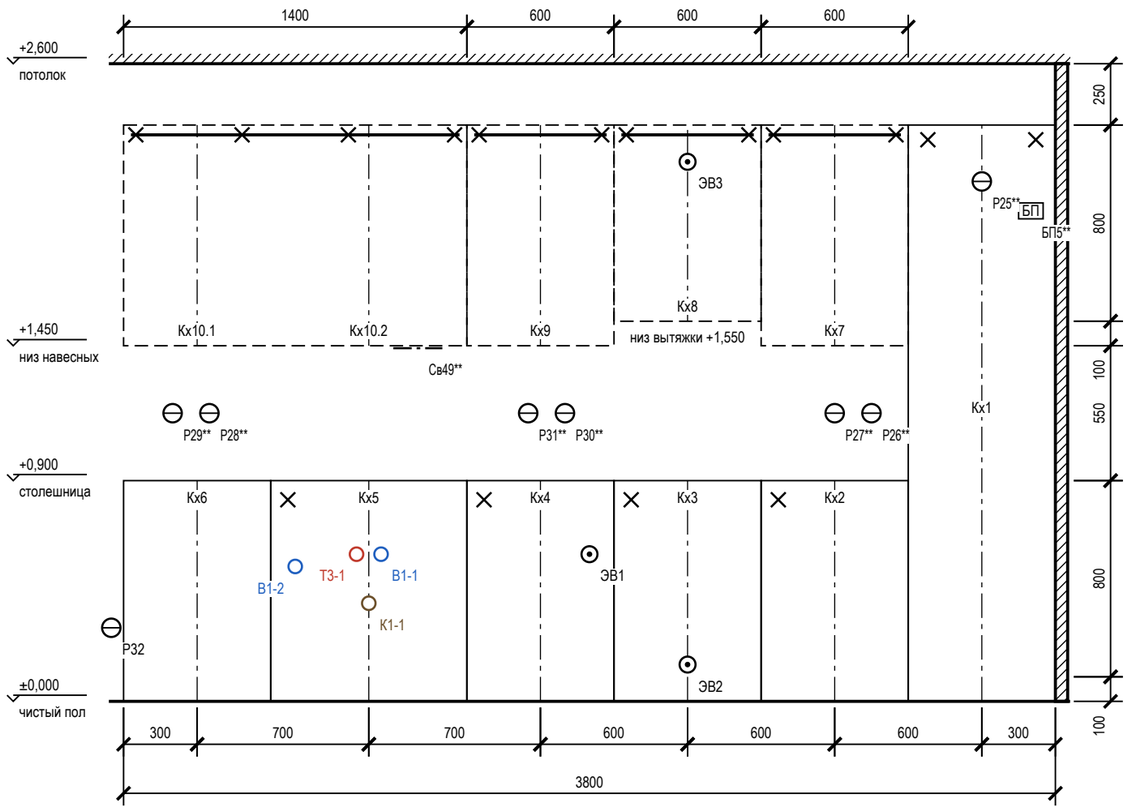

План столешницы (М 1:25)

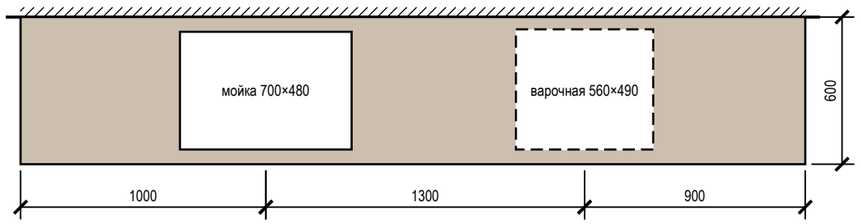

Привязка выводов к осям модулей

Код	Назначение	Модуль	От оси, мм	Н, мм	Размещение
Р32	розетка — посудомоечная машина (на стене за торцом гарнитура, доступ сбоку)			300	вне гарнитура
Р29**	розетка — фартук	Кх6	−100	1175	над столешницей (фартук)
Р28**	розетка ×2 — фартук	Кх6	+50	1175	над столешницей (фартук)
В1-2	В1 — кран ПММ в шкафу мойки	Кх5	−300	550	в модуле мойки
Т3-1	Т3 — межос. 100	Кх5	−50	600	в модуле мойки
К1-1	К1 Ø50 — мойка	Кх5	0	400	в модуле мойки
В1-1	В1 — межос. 100	Кх5	+50	600	в модуле мойки
Св49**	светодиодная лента — подсветка столешницы	Кх5	+200	1440	в профиле по низу навесного модуля
Р31**	розетка — фартук между мойкой и варочной	Кх4	−50	1175	над столешницей (фартук)
Р30**	розетка ×2 — фартук между мойкой и варочной	Кх4	+100	1175	над столешницей (фартук)
ЭВ1	вывод кабеля — варочная панель — в соседнем модуле, за ящиком	Кх4	+200	600	в соседнем модуле, за ящиком
ЭВ2	вывод кабеля — духовой шкаф	Кх3	0	150	под духовым шкафом, доступ через ящик
ЭВ3	вывод кабеля — вытяжка — над корпусом	Кх8	0	2200	в навесном модуле
Р27**	розетка — фартук	Кх2	0	1175	над столешницей (фартук)
Р26**	розетка ×2 — фартук	Кх2	+150	1175	над столешницей (фартук)
Р25**	розетка — холодильник — над нишей, съёмная панель	Кх1	0	2120	над нишей холодильника, съёмная панель
БП5**	блок питания — в колонне Кх1 над нишей холодильника, верх, съёмная панель	Кх1	+200	2000	над нишей холодильника, съёмная панель

Зазоры под отделку

Поверхность	Отделка	Зазор, мм	Учесть
фартук	керамогранит	10	от чернового основания до корпуса навесных и столешницы
стены	окраска	5	под штукатурку и шпаклёвку за пеналом
пол	инженерная доска		цоколь — после укладки пола, опоры ±20 мм

Условные обозначения

- нижний модуль, пенал (контур)
- невидимый контур: навесной модуль, корпус под столешницей
- ось модуля (от неё — привязка вывода)
- анкер / уголок крепления к стене
- розетка на стене
- вывод кабеля к технике
- В1 — вывод воды В1 / Т3, канализации К1

Примечания

1. Выводы — по проекту электрики и ВК; привязка по горизонтали — от оси модуля (плюс — вправо по виду), по высоте — от чистого пола до оси вывода.
2. Пенал — уголки к стене 2 шт. сверху; нижние модули — стяжками между собой и уголком к стене; ряд выставить по уровню опорами цоколя.
3. Розетки над столешницей — не ниже 150 мм над ней и не за корпусом техники; розетка за ПММ, духовым шкафом и холодильником — только в соседнем модуле или в зоне цоколя с доступом.
4. Столешница — вырезы по шаблонам выбранных моделей мойки и варочной панели; торцы у стены — герметик, пристеночный плинтус.

Допущения и предложения на листе

Основа листа: размеры помещений и положение проёмов введены заказчиком в брифе, на объекте не замерены (К-1); высота потолка 2700 мм — по брифу заказчика, не замерена (К-2); толщины стен приняты по брифу: наружные 200 мм, внутренние 150 мм — не обмерены (К-1); тип дома монолитный, перекрытие 200 мм — по брифу заказчика, документов нет (К-3); планировка (стены, проёмы, объединение кухни и гостиной, расширение санузла) — по брифу без обмера и плана БТИ (К-7); разрешённая мощность 10 кВт принята, ТУ не переданы (К-8); вентканалы приняты, в брифе не заданы (К-9); подрайон климата не задан — принят не северный (жилые от 2,5 м) (К-10).

Знак «**» — предложение проектировщика, заказчиком не утверждено (согласовать с заказчиком): Р25 — высота 2120 мм выше нормы 1 м (ПУЭ 6.6.30) по назначению: розетка встроенного прибора — в колонне Кх1 над нишей, в антресоли за съёмной панелью; Р26, Р27, Р28, Р29, Р30, Р31 — Сдвиг под раскладку плитки фартука (стена Г) на 75 мм выше — ось на шве или в центре плитки, привязка по таблице листа; Св49, БП5 — диммируемость добавлена разработчиком проекта под светорегуляторы S8 и S9.

См. лист открытых вопросов (лист 6, записи К-1–К-3, К-7–К-10).

1000 мм · печать 1:1

Изм.	Кол.уч	Лист	№ док.	Подп.	Дата
Разраб.		Кырлан А.С.			13.11.26
Пров.					
ГИП					
Н. контр.					
Утв.					

ГД-2026-011-АИ

Квартира 56 м²

ЖК «Северный парк», Москва

Дизайн-проект интерьера

Стадия	Лист	Листов
РП	77	119

Кухня (пом. 1). Монтажная схема

М 1:25

Кырлан Александр Сергеевич

выпуск 13.11.2026 № eb78108141 · стр. 85 из 139


ПРЕДВАРИТЕЛЬНО · не для производства работ · открыто пунктов: 13 (реестр — л. 6, 7)

Кухня (пом. 1). Столешница: план

Гостиная-кухня (пом. 1) · размеры в мм · вид сверху

План столешницы (вид сверху, стена вверху) М 1:20

Ст-1: стена D, 3200×600

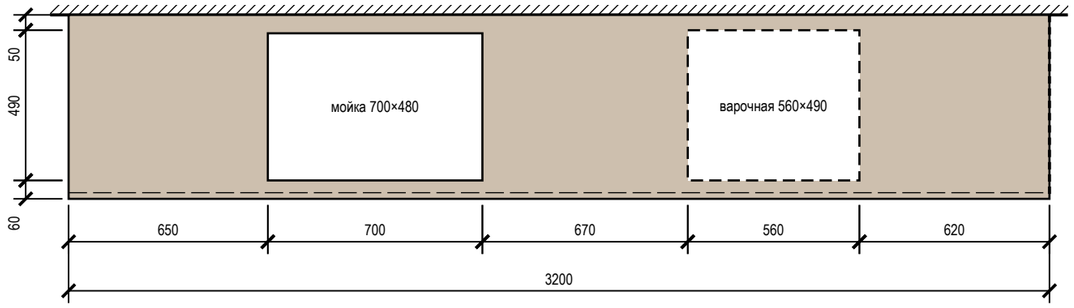

свес над фасадами 20 мм · толщина 38 мм*

Ведомость столешниц

Марка	Стена	Д×Ш×Т, мм	Материал	Вырезы	Кромка	Стыки
Ст-1	D	3200×600×38*	материал не задан (materials.worktop.mat	мойка 700×480; варочная 560×490	3,80 пог. м	нет
Итого			**S = 1,92 м²**		**3,80 пог. м**	

Примечания

1. Материал: материал не задан (materials.worktop.mat) (materials.worktop.mat в данных не задан); толщина 38 мм*.
2. * — толщина принята по практике (38 мм): в данных изделия materials.worktop.thk не задана.
3. Розеток в столешнице нет: питание над столешницей — на фартуке (план розеток), не за корпусом техники.
4. Вырезы: мойка — по габариту чаши 700×480 (прибор), отступ от стены 60 мм; варочная панель — ориентир 560×490 мм, отступ от стены 50 мм; вырезы разметить по шаблону выбранных моделей, углы выреза — радиус не менее 5 мм.
5. Радиусы углов и фаска кромки в данных не заданы: углы столешницы прямые, кромка — прямая без фаски, пока не задано иное.
6. Стыков нет: каждая столешница — одной деталью.
7. Свес над фасадами — 20 мм; торцы: свободный торец — кромка, торец у стены или пенала — зазор не более 3 мм, герметик. Длина кромки — по лицевой стороне и свободным торцам.

Допущения и предложения на листе

Основа листа: размеры помещений и положение проёмов введены заказчиком в брифе, на объекте не замерены (К-1); высота потолка 2700 мм — по брифу заказчика, не замерена (К-2); толщины стен приняты по брифу: наружные 200 мм, внутренние 150 мм — не обмерены (К-1); тип дома монолитный, перекрытие 200 мм — по брифу заказчика, документов нет (К-3); планировка (стены, проёмы, объединение кухни и гостиной, расширение санузла) — по брифу без обмера и плана БТИ (К-7); разрешённая мощность 10 кВт принята, ТУ не переданы (К-8); вентканалы приняты, в брифе не заданы (К-9); подрайон климата не задан — принят не северный (жилые от 2,5 м) (К-10).

См. лист открытых вопросов (лист 6, записи К-1–К-3, К-7–К-10).

1000 мм · печать 1:1

						ГД-2026-011-АИ	
						Квартира 56 м²	
						ЖК «Северный парк», Москва	
Изм.	Кол.уч	Лист	№ док.	Подп.	Дата		
Разраб.		Кырлан А.С.			13.11.26	Дизайн-проект интерьера	Стадия: РП; Лист: 78; Листов: 119
Пров.							
ГИП							
						Кухня (пом. 1). Столешница: план М 1:20	**Кырлан Александр Сергеевич**
Н. контр.							
Утв.							


выпуск 13.11.2026 № eb7810814f · стр. 86 из 139

Шкафы. Монтажная схема


крепление к стене, установочные размеры, зазоры под отделку · размеры в мм

ПРЕДВАРИТЕЛЬНО · не для производства работ · открыто пунктов: 13 (реестр — л. 6, 7)


Шкаф распашной Сп4 (пом. 2) (М 1:25)

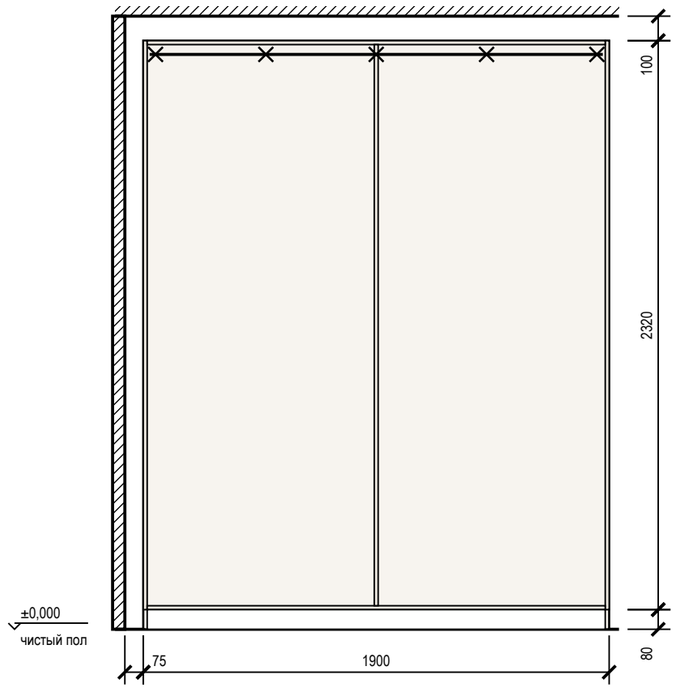


Шкаф распашной Дт2 (пом. 3) (М 1:25)

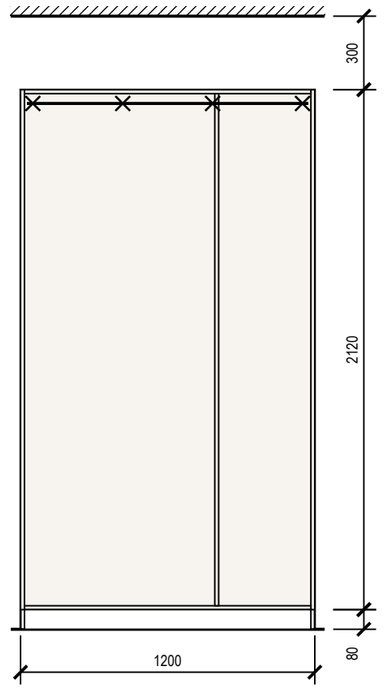

Шкаф-купе Пр1 (пом. 5) (М 1:25)

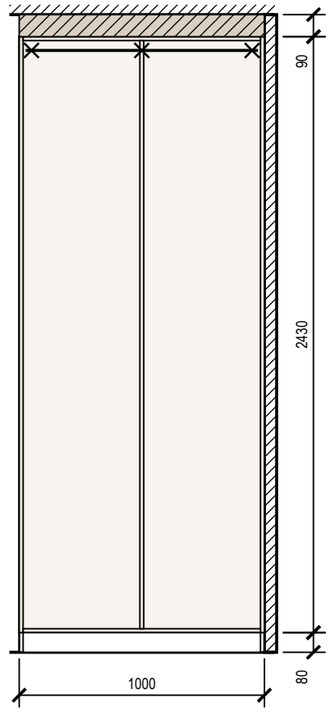

Система хранения Пр3 (пом. 5) (М 1:25)

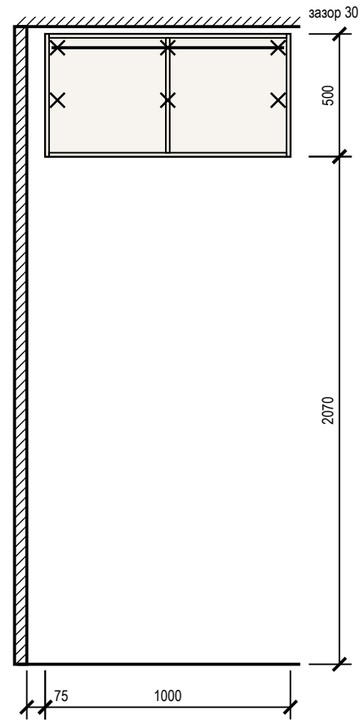

Допущения и предложения на листе

Основа листа: размеры помещений и положение проёмов введены заказчиком в брифе, на объекте не замерены (К-1); высота потолка 2700 мм — по брифу заказчика, не замерена (К-2); толщины стен приняты по брифу: наружные 200 мм, внутренние 150 мм — не обмерены (К-1); тип дома монолитный, перекрытие 200 мм — по брифу заказчика, документов нет (К-3); планировка (стены, проёмы, объединение кухни и гостиной, расширение санузла) — по брифу без обмера и плана БТИ (К-7); разрешённая мощность 10 кВт принята, ТУ не переданы (К-8); вентканалы приняты, в брифе не заданы (К-9); подрайон климата не задан — принят не северный (жилые от 2,5 м) (К-10).

См. лист открытых вопросов (лист 6, записи К-1–К-3, К-7–К-10).

Крепление и зазоры под отделку

Марка	Помещение, стена	Основание	Отделка стены	Зазор, мм	Крепёж по планке	От опрокидывания
Сп4	Спальня (2), стена В	по основанию — см. таблицу крепежа	окраска	5	анкер 5 шт., шаг 450	уголок к стене, 2 шт.
Дт2	Детская (3), стена А	по основанию — см. таблицу крепежа	окраска	5	анкер 4 шт., шаг 367	уголок к стене, 2 шт.
Пр1	Прихожая (5), стена В	по основанию — см. таблицу крепежа	окраска	5	анкер 3 шт., шаг 450	уголки 2 шт.
Пр3	Прихожая (5), стена В	по основанию — см. таблицу крепежа	окраска	5	анкер 6 шт. (2 ряда)	уголки 2 шт.

Крепёж по основанию стены

Основание стены	Крепёж
бетон, ж/б	анкер-шуруп 7,5×72 или дюбель 8×60 с шурупом 5×70
кирпич полнотелый	дюбель 8×80 с шурупом 5×90
газобетон, пазогребень	дюбель для газобетона 10×100 или химический анкер
гипсокартон	закладная до обшивки (брус 40×80 или фанера 18 мм), саморез в закладную

Условные обозначения

- × — анкер / уголок крепления к стене
- корпус и полки ЛДСП (вид на стену)
- компенсатор — короб до потолка

Примечания

1. Установочные размеры — от чистого пола и чистых стен; перед установкой контрольный замер после отделки.
2. Порядок: корпус выставить по уровню опорами цоколя → закрепить к стене по задней планке → навесить двери и фасады, отрегулировать зазоры → подогнать и закрепить компенсатор.
3. Анкеры — с шагом не более 500 мм, не ближе 50 мм от края планки; на ГКЛ только в закладную, установленную до обшивки.
4. Скрытые коммуникации под анкеры проверить детектором; трассы электрики по плану розеток.

1000 мм · печать 1:1

Изм.	Кол.уч	Лист	№ док.	Подп.	Дата
Разраб.		Кырлан А.С.			13.11.26
Пров.					
ГИП					
Н. контр.					
Утв.					

ГД-2026-011-АИ

Квартира 56 м²

ЖК «Северный парк», Москва

Дизайн-проект интерьера

Стадия	Лист	Листов
РП	79	119

Шкафы. Монтажная схема

М 1:25

Кырлан Александр Сергеевич

выпуск 13.11.2026 № eb78108141 · стр. 87 из 139

Ведомости изделий, техники и фурнитуры

встроенная мебель и кухонный гарнитур · размеры в мм

Ведомость изделий

Марка	Наименование	Пом.	Ш×Г×В, мм	Корпус	Фасад	Кромка, мм	Кол.
Сп4	Шкаф распашной	2	1900×600×2400	ЛДСП 16	МДФ 18 мм, эмаль матовая	0,4 / 2	1
Дт2	Шкаф распашной	3	1200×600×2200	ЛДСП 16	МДФ 18 мм, эмаль матовая	0,4 / 2	1
Пр1	Шкаф-купе	5	1000×600×2510	ЛДСП 16	ЛДСП 10 мм, декор «дуб натуральный» в профиле: алюминий, чёрный матовый; вставка — зеркало серебро 4 мм, плёнка безопасности	0,4 / 2	1
Пр3	Система хранения	5	1000×400×500	ЛДСП 16	без фасадов	0,4 / 2	1
Кх6	Модуль под ПММ 60: без корпуса, фасад на дверь машины	1	600×600×900	без корпуса	МДФ 18 мм, эмаль матовая — на дверь машины (навеска из её комплекта), цоколь		1
Кх10	Модуль навесной: полки, сушка	1	1400×350×900	ЛДСП 16	МДФ 18 мм, эмаль матовая	0,4 / 2	1
Кх5	Модуль нижний: мойка	1	800×600×900	ЛДСП 16	МДФ 18 мм, эмаль матовая	0,4 / 2	1
Кх4	Модуль нижний: ящики	1	600×600×900	ЛДСП 16	МДФ 18 мм, эмаль матовая	0,4 / 2	1
Кх9	Модуль навесной: полки	1	600×350×900	ЛДСП 16	МДФ 18 мм, эмаль матовая	0,4 / 2	1
Кх3	Модуль нижний: духовой шкаф, варочная	1	600×600×900	ЛДСП 16	МДФ 18 мм, эмаль матовая	0,4 / 2	1
Кх8	Модуль навесной: полки	1	600×350×800	ЛДСП 16	МДФ 18 мм, эмаль матовая	0,4 / 2	1
Кх2	Модуль нижний: ящики	1	600×600×900	ЛДСП 16	МДФ 18 мм, эмаль матовая	0,4 / 2	1
Кх7	Модуль навесной: полки	1	600×350×900	ЛДСП 16	МДФ 18 мм, эмаль матовая	0,4 / 2	1
Кх1	Пенал: холодильник встр.	1	600×650×2350	ЛДСП 16	МДФ 18 мм, эмаль матовая	0,4 / 2	1

Ведомость встраиваемой техники

Поз.	Прибор	Ниша, вырез, мм	Вентиляция	Питание	Схема
Кх6	Посудомоечная машина встраиваемая, 60 см	ниша 600 × 862 (от пола до низа столешницы)	зазор в цоколе, по схеме	Р32: —, Н=300 — вне гарнитура	по модели
Кх5	Мойка врезная / подстольная с сифоном	вырез по шаблону, ориентир 700 × 480		смеситель — выводы ВК	по модели
Кх3	Духовой шкаф встраиваемый, 60 см	ниша 560 × 600, глубина ≥ 550	зазор за шкафом, вырез в задней стенке	ЭВ2: Кх3, Н=150 — под духовым шкафом, доступ через ящик	по модели
Кх3	Варочная панель индукционная, 60 см	вырез в столешнице 560 × 490		ЭВ1: Кх4, Н=600 — в соседнем модуле, за ящиком	по модели
Кх1	Холодильник встраиваемый, ниша 1780	ниша 1780 × 560 × 550	решётка в цоколе, канал за корпусом, выход сверху	Р25**: Кх1, Н=2120 — над нишей холодильника, съёмная панель	по модели
Кх8	Вытяжка встраиваемая в навесной модуль, 60 см	низ ≥ 650 над панелью	воздуховод к вентканалу, короб до потолка	ЭВ3: Кх8, Н=2200 — в навесном модуле	по модели

Ведомость фурнитуры

№	Фурнитура	Тип, размер	Изделия	Кол.
1	Петля накладная 110° с доводчиком	чашка 35 мм	Сп4, Дт2, Кх10, Кх5, Кх9, Кх8, Кх7, Кх1	73
2	Полкодержатель с фиксацией	ø5 мм	Сп4, Дт2, Пр1, Кх10, Кх9, Кх8, Кх7, Кх1	96
3	Штанга овальная 30×15, L = 926	+ 2 держателя	Сп4	1
4	Опора регулируемая с цоколем на клипсах	ход 20 мм	Сп4, Дт2, Пр1	20
5	Анкер по основанию стены	по таблице крепежа	Сп4, Дт2, Пр1, Пр3, Кх10, Кх9, Кх8, Кх7	28
6	Уголок крепления к стене от опрокидывания	стальной	Сп4, Дт2, Пр1, Пр3, Кх1	10
7	Штанга овальная 30×15, L = 776	+ 2 держателя	Дт2	1
8	Система дверей купе: профиль, направляющие, ролики	на 2 двери	Пр1	1
9	Ручка-профиль вертикальная	в цвет профиля	Пр1	2
10	Штанга овальная 30×15, L = 476	+ 2 держателя	Пр1	1
11	Полка для обуви выдвижная наклонная	ширина 476	Пр1, Пр3	7
12	Ручка-профиль	латунь матовая	Кх6, Кх10, Кх5, Кх4, Кх9, Кх3, Кх8, Кх2, Кх7, Кх1	23
13	Комплект навески фасада ПММ	из поставки машины	Кх6	1
14	Сушка для посуды в шкаф	ширина 800	Кх10	1
15	Навес регулируемый для навесного шкафа	пара на секцию	Кх10, Кх9, Кх8, Кх7	5
16	Шина монтажная	L = 1340	Кх10	1
17	Опора кухонная регулируемая 100–120 мм	+ клипса цоколя	Кх5, Кх4, Кх3, Кх2, Кх1	22
18	Направляющие полного выдвижения с доводчиком NL 500	пара	Кх4, Кх3, Кх2	7
19	Шина монтажная	L = 540	Кх9, Кх8, Кх7	3

Примечания

1. Модели техники выбирает заказчик до изготовления мебели; ниши, вырезы и вентиляция — по монтажной схеме выбранной модели (условие гарантии), её номер вносится в ведомость.
2. Количество фурнитуры — по чертежам изделий; запас крепежа 5 %. Аналоги — по характеристикам (доводчик, нагрузка, ход).
3. Цвет корпусов, фасадов и профилей — по колерной карте проекта. Кромка — скрытые / видимые торцы, мм.

Допущения и предложения на листе

Основа листа: размеры помещений и положение проёмов введены заказчиком в брифе, на объекте не замерены (К-1); высота потолка 2700 мм — по брифу заказчика, не замерена (К-2); толщины стен приняты по брифу: наружные 200 мм, внутренние 150 мм — не обмерены (К-1); тип дома монолитный, перекрытие 200 мм — по брифу заказчика, документов нет (К-3); планировка (стены, проёмы, объединение кухни и гостиной, расширение санузла) — по брифу без обмера и плана БТИ (К-7); разрешённая мощность 10 кВт принята, ТУ не переданы (К-8); вентканалы приняты, в брифе не заданы (К-9); подрайон климата не задан — принят не северный (жилые от 2,5 м) (К-10).

Знак «**» — предложение проектировщика, заказчиком не утверждено (согласовать с заказчиком): Р25 — высота 2120 мм выше нормы 1 м (ПУЭ 6.6.30) по назначению: розетка встроенного прибора — в колонне Кх1 над нишей, в антресоли за съёмной панелью.

См. лист открытых вопросов (лист 6, записи К-1–К-3, К-7–К-10).

Изм.	Кол.уч	Лист	№ док.	Подп.	Дата
Разраб.		Кырлан А.С.			13.11.26
Пров.					
ГИП					
Н. контр.					
Утв.					

ГД-2026-011-АИ

Квартира 56 м²

ЖК «Северный парк», Москва

Дизайн-проект интерьера

Стадия	Лист	Листов
РП	80	119

Ведомости изделий, техники и фурнитуры

М б/м

Кырлан Александр Сергеевич

выпуск 13.11.2026 № eb7810814f · стр. 88 из 139

ПРЕДВАРИТЕЛЬНО · не для производства работ · открыто пунктов: 13 (реестр — л. 6, 7)

Сводка листовых материалов и кромки

ЛДСП, МДФ, ХДФ и кромка по изделиям · площади в м², кромка в пог. м

Листовые материалы по толщинам и декорам

Материал, декор	Назначение	Изделий	S, м²	S × 1,15*, м²
ЛДСП 16 мм*	корпус	13	39,71	45,66
ХДФ 4 мм	задняя стенка	13	16,03	18,44
МДФ 18 мм, эмаль матовая	фасад	12	13,05	15,01
ЛДСП 10 мм в алюминиевом профиле	фасад	1	2,35	2,71
Итого			**71,15**	**81,82**

Кромка по типам

Кромка	Толщина, мм	Длина, пог. м	+10 %*, пог. м
видимая (передний торец, торец фасада ЛДСП)	2	98,8	108,6
скрытая (задний торец деталей корпуса)	0,4	75,2	82,7

Примечания

1. Площади — по моделям изделий листов мебельщика: боковины, дно, крыша (у нижнего кухонного модуля — дно и две царги по 100 мм), полки, стойки, задняя стенка ХДФ, цоколь, фасады. Коэффициент раскроя 1,15* — обрезь, пропилы и подбор рисунка; сводка — для заказа материала, раскрой делает цех.
2. Кромка: видимая — передний торец деталей корпуса и периметр фасада из ЛДСП; скрытая — задний торец деталей корпуса. Фасады из МДФ (эмаль, шпон) кромки не имеют. Толщина — из materials.edge изделий; где не задана — по умолчанию 2 и 0,4 мм*.
3. Не вошло: короба ящиков (в комплекте направляющих NL), столешница (лист «Столешница: план» и раскрой камня), остров, встроенная техника, покупные изделия.
4. Мягкое изголовье Сп1 (пом. 2): чертёж не выпущен — в данных нет ширина панели, отметка верха от пола (headboard), высота панели, толщина панели, членение и стёжка (шаг, рисунок) или «гладкая обивка» (plain), ткань (headboardSpec.fabric) (записи реестра нет).
5. * — значение принято по практике, не задано в данных.

Изделия (14)

Изделие	Пом.	Корпус, м²	ХДФ, м²	Фасад, м²	Кромка, пог. м
Сп4 Шкаф распашной	2	9,46	4,41	4,37	34,3
Дт2 Шкаф распашной	3	6,62	2,54	2,52	23,8
Пр1 Шкаф-купе	5	7,18	2,43	2,35	37,4
Пр3 Система хранения	5	1,36	0,50	0,00	6,8
Кх6 модуль кухни	1	0,00	0,00	0,45	0,0
Кх10 модуль кухни	1	2,16	1,26	1,24	13,3
Кх5 модуль кухни	1	1,52	0,61	0,60	6,9
Кх4 модуль кухни	1	1,35	0,46	0,45	5,9
Кх9 модуль кухни	1	1,15	0,54	0,53	7,0
Кх3 модуль кухни	1	1,35	0,46	0,10	5,9
Кх8 модуль кухни	1	1,09	0,48	0,47	6,6
Кх2 модуль кухни	1	1,35	0,46	0,45	5,9
Кх7 модуль кухни	1	1,15	0,54	0,53	7,0
Кх1 модуль кухни	1	3,97	1,35	1,34	13,0

Допущения и предложения на листе

Основа листа: размеры помещений и положение проёмов введены заказчиком в брифе, на объекте не замерены (К-1); высота потолка 2700 мм — по брифу заказчика, не замерена (К-2); толщины стен приняты по брифу: наружные 200 мм, внутренние 150 мм — не обмерены (К-1); тип дома монолитный, перекрытие 200 мм — по брифу заказчика, документов нет (К-3); планировка (стены, проёмы, объединение кухни и гостиной, расширение санузла) — по брифу без обмера и плана БТИ (К-7); разрешённая мощность 10 кВт принята, ТУ не переданы (К-8); вентканалы приняты, в брифе не заданы (К-9); подрайон климата не задан — принят не северный (жилые от 2,5 м) (К-10).

Знак «**» — предложение проектировщика, заказчиком не утверждено (согласовать с заказчиком): плинтус пом. 1, 2, 5, фартук пом. 1 — артикул изделия не выбран: позиция описана характеристиками («аналог по характеристикам»), артикул выбирается при закупке; пол пом. 4 — пирог пола: стяжка 33 мм и обмазочная гидроизоляция добавлены разработчиком проекта; артикул изделия не выбран: позиция описана характеристиками («аналог по характеристикам»), артикул выбирается при закупке.

См. лист открытых вопросов (лист 6, записи К-1–К-3, К-7–К-10).

Изм.	Кол.уч	Лист	№ док.	Подп.	Дата
Разраб.		Кырлан А.С.			13.11.26
Пров.					
ГИП					
Н. контр.					
Утв.					

ГД-2026-011-АИ

Квартира 56 м²

ЖК «Северный парк», Москва

Дизайн-проект интерьера

Стадия	Лист	Листов
РП	81	119

Сводка листовых материалов и кромки

М б/м

Кырлан Александр Сергеевич

09

Развёртки и узлы

Кырлан Александр Сергеевич

выпуск 13.11.2026 · eb7810814f · стр. 90 из 139

Реестр марок отделки и позиций альбома

Реестр марок отделки (О ↔ позиции колерной карты) и марки позиций по видам

ПРЕДВАРИТЕЛЬНО · не для производства работ · открыто пунктов: 13 (реестр — л. 6, 7)

Реестр марок отделки альбома

Марка	Поверхность	Материал, изделие	Цвет, код	Помещения	Колер. карта
О1	стены	окраска, Tikkurila Euro Power 7, колеровка по NCS, матовая, подготовка Q3	NCS S 0804-Y30R «S 0804-Y30R»	1, 2, 3, 5	К1
О2	фартук	керамогранит, 1200×600×9 мм, аналог: керамогранит под травертин, матовый, затирка CG2WA		1	КМ2
О3	акцентная стена	окраска, Farrow & Ball Modern Emulsion, матовая, подготовка Q3	Farrow & Ball No. 298 «Bancha»	1	К2
О4	плинтус	плинтус МДФ, h 80 мм, аналог: плинтус МДФ под покраску 80×16	NCS S 0804-Y30R «S 0804-Y30R»	1, 2, 5	К4
О5	потолок	окраска, Tikkurila Euro Power 7, глубокоматовая, подготовка Q3	Tikkurila F485 «Damask»	1, 2, 3, 4, 5	К3, К8
О6	пол	инженерная доска, Coswick Классическая, 2100×127 мм, 1167-1101		1, 2, 3	КМ1
О7	акцентная стена	окраска, Tikkurila Euro Power 7, колеровка по NCS, матовая, подготовка Q3	NCS S 5010-G70Y «S 5010-G70Y»	2	К5
О8	акцентная стена	окраска, Tikkurila Euro Power 7, матовая, подготовка Q3	Tikkurila X447 «Sea Smoke»	3	К6
О9	плинтус	плинтус МДФ, Orac Decor Contour (Luxxus), h 69 мм, SX165	NCS S 0804-Y30R «S 0804-Y30R»	3	К7
О10	стены	облицовка плиткой, Atlas Concorde Marvel Travertine, 600×1200×9 мм, A8UZ, затирка CG2WA	Atlas Concorde A8UZ «Marvel Travertine»	4	КМ3
О11	пол	керамогранит, 600×600×9 мм, аналог: керамогранит ректифицированный под травертин, матовый, затирка CG2WA		4	КМ4
О12	пол	керамогранит, Atlas Concorde Marvel Travertine, 600×1200×9 мм, A8UZ, затирка CG2WA	Atlas Concorde A8UZ «Marvel Travertine»	5	КМ5

Марки позиций альбома по видам

Префикс	Что обозначает, позиции	Листы
Д	двери: Д-1–Д-5	21–25
ОК	окна: ОК-1–ОК-3	21–25
Гс, Дт, Кх, Пр, Сп	мебель и оборудование: Гс1–Гс3, Гс4**, Гс5**, Дт1, Дт2, Дт3**, Дт4, Дт5, Кх1–Кх11, Пр1–Пр3, Сп1–Сп6	26–31
П, Сн	сантехнические приборы: П1, П2, Сн1–Сн5	43–50
ДК, ДС	декор (картины, зеркала, растения): ДК1–ДК8, ДК9**, ДК10**, ДК11**, ДК12**, ДК13**, ДК14**, ДК15**, ДК16**, ДК17**, ДК18**, ДС1**	1, 64–69
Т	текстиль (шторы, ковры): Т1–Т14, Т16–Т19, Т20**, Т21**, Т22**	1, 64–69
S	выключатели: S1–S7, S8**, S9**, S10, S11, S12**, S13**	32–40
Р	розетки: Р1–Р6, Р7**, Р8**, Р9, Р11, Р13–Р16, Р17**, Р18**, Р19**, Р20–Р24, Р25**, Р26**, Р27**, Р28**, Р29**, Р30**, Р31**, Р32	32–40
ТВ	розетки ТВ: ТВ1	32–40
LAN	розетки компьютерные: LAN1–LAN3	32–40
ЭВ	выводы кабеля: ЭВ1–ЭВ3, ЭВ4**, ЭВ6**	32–40
АР	точки доступа Wi-Fi: АР1**, АР2**	32–40

Марки позиций альбома по видам (продолжение)

Префикс	Что обозначает, позиции	Листы
Св	светильники: Св1–Св14, Св15**, Св17–Св29, Св30**, Св31**, Св32**, Св33**, Св34**, Св35**, Св36**, Св37**, Св38**, Св41, Св42**, Св43**, Св44**, Св45–Св48, Св49**	32–40
БП	блоки питания LED: БП1–БП4, БП5**	32–40
ИП	извещатели: ИП1–ИП5	32–40
КУП	электроустановочные изделия: КУП1**	32–40
ЩК, ЩС**	щиты: ЩК, ЩС**	32–40
ДФ	домофон: ДФ1	32–40
Ст В1, Ст К1	стояки (системы В1, Т3, К1): Ст В1-1*, Ст К1-1*	43–50
О	марки отделки (реестр альбома): О1–О12	2–5, 82–103
К, КМ	позиции колерной карты: К1–К8, КМ1–КМ5	62, 63
РО	радиаторы отопления: РО-1–РО-3	41, 42

Примечания

1. Марка отделки О — одна на весь альбом: одна и та же отделка (материал, изделие, цвет, формат) на всех листах имеет одну марку; на развёртках и планах стоят марки этого реестра.
2. Столбец «Колер. карта» — позиции колерной карты (лист 62): К — окраска по коду цвета, КМ — материал без кода цвета; «Помещения» — номера по экспликации; количества — по ведомости отделки помещений (лист 61).
3. Марки позиций: один префикс — один вид позиций на весь альбом (двери Д, окна ОК, мебель М, сантехприборы П, декор ДК, текстиль Т, колерная карта К и КМ, радиаторы РО, розетки Р, выключатели S, светильники Св; стояки — «Ст» и система, например «Ст К1-1*»). Совпадение префиксов у разных видов — замечание к исходным данным, при выпуске исправляется в модели.

Допущения и предложения на листе. Основа листа: размеры помещений и положение проёмов введены заказчиком в брифе, не замерены (К-1); высота потолка 2700 мм — по брифу заказчика, не замерена (К-2); толщины стен приняты по брифу: наружные 200 мм, внутренние 150 мм — не обмерены (К-1); тип дома монолитный, перекрытие 200 мм — по брифу заказчика, документов нет (К-3); планировка (стены, проёмы, объединение кухни и гостиной, расширение санузла) — по брифу без обмера и плана БТИ (К-7); разрешённая мощность 10 кВт принята, ТУ не переданы (К-8); вентканалы приняты, в брифе не заданы (К-9); подрайон климата не задан — принят не северный (жилые от 2,5 м) (К-10). Знак «*» — принято, не замерено (замерить): К-4: Ст К1-1, Ст В1-1. Знак «**» — предложено, не утверждено (согласовать): плинтус пом. 1, 2, 5, фартук пом. 1, пол пом. 4, S12, S8, S13, S9, P18, P19, P25, P26, P27, P28, P29, P30, P31, Св31, Св32, Св33, Св34, Св35, Св36, Св37, Св38, Св42, Св43, Св44, Св49, БП5, ДС1, Р7, Р8, Св15, ЭВ4, КУП1, ЭВ6, Р17, Св30, АР2, ЩС, АР1; ИЗ-1: Гс4; ИЗ-1–ИЗ-3: Дт3; ИЗ-1, ИЗ-3: Гс5. См. лист открытых вопросов (лист 6, записи К-1–К-4, К-7–К-10; лист 7, записи ИЗ-1–ИЗ-3).

						ГД-2026-011-АИ	
						Квартира 56 м²	
Изм.	Кол.уч	Лист	№ док.	Подп.	Дата	ЖК «Северный парк», Москва	
Разраб.		Кырлан А.С.			13.11.26	Дизайн-проект интерьера	Стадия: РП; Лист: 82; Листов: 119
Пров.							
ГИП							
Н. контр.						**Реестр марок отделки и позиций альбома** М б/м	**Кырлан Александр Сергеевич**
Утв.							

выпуск 13.11.2026 № eb7810814f · стр. 91 из 139

Схема расположения развёрток и узлов

План квартиры: марки развёрток по помещениям, выноски узлов, ведомость «марка → лист»

ПРЕДВАРИТЕЛЬНО · не для производства работ · открыто пунктов: 13 (реестр — л. 6, 7)



Развёртки и узлы: марка → лист

Марка	Помещение / узел	Лист
Г	Гостиная-кухня (пом. 1)	84
А	Гостиная-кухня (пом. 1)	85
Б	Гостиная-кухня (пом. 1)	86
В	Гостиная-кухня (пом. 1)	87
А	Спальня (пом. 2)	88
Б	Спальня (пом. 2)	89
В	Спальня (пом. 2)	90
Г	Спальня (пом. 2)	91
А	Детская (пом. 3)	92
Б, Г	Детская (пом. 3)	93
В	Детская (пом. 3)	94
А	Санузел (пом. 4)	95
Б	Санузел (пом. 4)	96
В, Г	Санузел (пом. 4)	97
А	Прихожая (пом. 5)	98
Б	Прихожая (пом. 5)	99
В	Прихожая (пом. 5)	100
Г	Прихожая (пом. 5)	101
узел 1	Порог 15 мм: мокрая зона — смежное помещение	102
узел 2	Стык покрытий пола Т-профилем без перепада	102
узел 3	Дверь скрытого монтажа в плоскости стены, плинтус	102
узел 4	Короб стояков К1-1 с люком и звукоизоляцией	102
узел 5	Гидроизоляция санузла: заход на стены 200 мм, примыкание ванны	103
узел 6	Плинтус МДФ 80×16 мм у окрашенной стены по доске (ламинату)	103
узел 7	Плинтус МДФ 80×16 мм у окрашенной стены по керамограниту (плитке)	103

Допущения и предложения на листе. Основа листа: размеры помещений и положение проёмов введены заказчиком в брифе, на объекте не замерены (К-1); высота потолка 2700 мм — по брифу заказчика, не замерена (К-2); толщины стен приняты по брифу: наружные 200 мм, внутренние 150 мм — не обмерены (К-1); тип дома монолитный, перекрытие 200 мм — по брифу заказчика, документов нет (К-3); планировка (стены, проёмы, объединение кухни и гостиной, расширение санузла) — по брифу без обмера и плана БТИ (К-7); разрешённая мощность 10 кВт принята, ТУ не переданы (К-8); вентканалы приняты, в брифе не заданы (К-9); подрайон климата не задан — принят не северный (жилые от 2,5 м) (К-10). Знак «*» — принято, не замерено и не подтверждено (замерить на объекте): К-4: Ст К1-1 — положение стояка канализации — по брифу заказчика, не замерено; Ст В1-1 — положение стояка холодной воды — по брифу заказчика, не замерено. Знак «**» — предложение проектировщика, заказчиком не утверждено (согласовать с заказчиком). См. лист открытых вопросов (лист 6, записи К-1–К-5, К-7–К-10).

Условные обозначения

- А — марка развёртки: буква стены, стрелка — взгляд
- выноска узла: над полкой — узел, под полкой — лист
- 1 — номер помещения, площадь м²

1000 мм · печать 1:1

Примечания

1. Развёртки — вид на стену изнутри помещения; буквы стен — одна система на весь альбом (как на листах выводов, плитки и отделки).
2. Стены без электроточек, мебели, декора и акцентной отделки развёрток не имеют: их отделка — по ведомости отделки помещений.
3. Узлы — на листе узлов; места применения — по выноскам этого листа и ведомости «марка → лист».

Изм.	Кол.уч	Лист	№ док.	Подп.	Дата
Разраб.		Кырлан А.С.			13.11.26
Пров.					
ГИП					
Н. контр.					
Утв.					

ГД-2026-011-АИ

Квартира 56 м²

ЖК «Северный парк», Москва

Дизайн-проект интерьера

Стадия	Лист	Листов
РП	83	119

Схема расположения развёрток и узлов

М 1:50

Кырлан Александр Сергеевич


выпуск 13.11.2026 № eb7810814f · стр. 92 из 139

Развёртка стены Г. Гостиная-кухня (пом. 1), кухонный фронт

ПРЕДВАРИТЕЛЬНО · не для производства работ · открыто пунктов: 13 (реестр — л. 6, 7)

Гостиная-кухня (пом. 1) · вид изнутри помещения · размеры в мм, отметки в м

Стена Г (М 1:20)

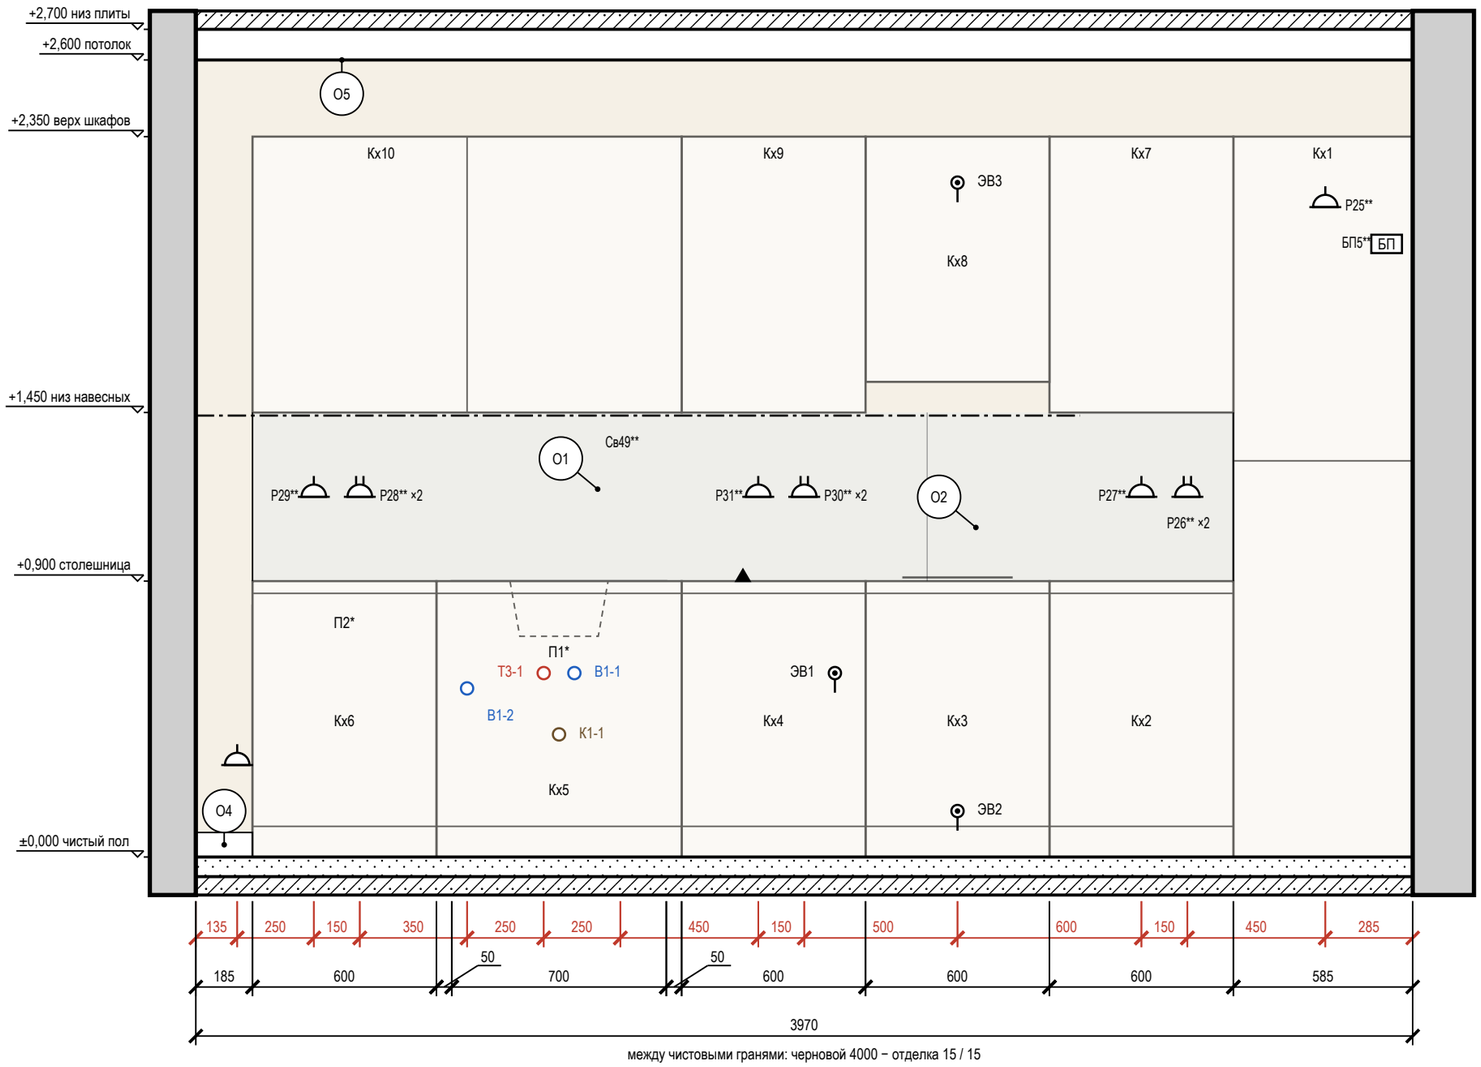

Ведомость точек и выводов

Марка	Что это	Гр.	H, мм	От угла, мм	Примечание
Р32	розетка: посудомоечная машина (на стене за торцом гарнитура, доступ сбоку)	10	300	135	
Р29**	розетка: фартук	7	1175	385	
Р28**	розетка: фартук	7	1175	535	рамка 2 поста
В1-2	холодная вода — посудомоечная машина		550*	885	кран ПММ в шкафу мойки
Т3-1	горячая вода — мойка кухонная		600*	1135	межос. 100
К1-1	канализация — мойка кухонная		400*	1185	Ø50
В1-1	холодная вода — мойка кухонная		600*	1235	межос. 100
Св49**	светильник настенный	2	1440	1385	лента -115–2885 от угла
Р31**	розетка: фартук между мойкой и варочной	7	1175	1835	
Р30**	розетка: фартук между мойкой и варочной	7	1175	1985	рамка 2 поста
ЭВ1	вывод кабеля: варочная панель — в соседнем модуле, за ящиком	8	600	2085	
ЭВ2	вывод кабеля: духовой шкаф	9	150	2485	
ЭВ3	вывод кабеля: вытяжка — над корпусом	11	2200	2485	
Р27**	розетка: фартук	7	1175	3085	
Р26**	розетка: фартук	7	1175	3235	рамка 2 поста
Р25**	розетка: холодильник — над нишей, съёмная панель	11	2120	3685	
БП5**	блок питания LED: в колонне Кх1 над нишей холодильника, верх, съёмная панель	2	2000	3885	

Условные обозначения

- розетка с заземляющим контактом; у знака марка, ×N — постов в рамке, гр. — группа щита, H — высота оси, мм
- вывод кабеля для подключения прибора (без розетки), марка ЭВ
- светодиодная лента в профиле / в карнизе короба
- БП — блок питания LED, с доступом (люк от 100×100 мм)
- вывод В1 (код — в ведомости привязок)
- вывод Т3 (код — в ведомости привязок)
- вывод К1 (код — в ведомости привязок)
- привязки точек и выводов от угла и от пола, мм
- мебель и приборы — фасад по расстановке (условно)
- стены и перекрытия в сечении
- плитка: сетка швов по формату, ▲ — ось старта
- окраска: тон — цвет по коду производителя (условно)
- О1 — марка отделки по реестру отделки альбома
- А — марка развёртки: буква стены, стрелка взгляд

Примечания

1. Развёртки — вид на стену изнутри помещения, по часовой стрелке; расположение — на листе 83; размеры — в мм по чистовым поверхностям; отметки — в м от ±0,000; высоты H — от чистого пола помещения до оси изделия, у декора — до центра.
2. Красная цепочка — привязки электроточек и выводов по осям от угла чистовых стен; высота H — у знака, от чистого пола до оси; высоты мебели, проёмов и границ отделки — колонкой отметок слева. У знака — короткая марка; назначение, группа щита, высота и привязка каждой точки и вывода — в «Ведомости точек и выводов» под видами (каждая точка — строка).
3. Отделка стен — по ведомости отделки помещений, лист 61.
4. У знака электроточки: марка (Р — розетка, S — выключатель, Св — светильник, ЭВ — вывод кабеля), ×N — число постов в рамке, гр. — группа щита, H — высота оси от чистого пола, мм; группы по клавишам выключателя — на листе выключателей.
5. Схема мебели, приборов и декора не является технической документацией для производства мебели; габариты — по паспортам изделий (* — высота не задана в проекте, показана по типовому изделию).
6. Выводы ВК — коды и высоты по листу выводов сантехники; * — высота принята по типовой практике монтажа, окончательно — по паспорту прибора.
7. Выводы кухонной техники — по утверждённому проекту кухни: привязки выводов даются от осей модулей гарнитура.
8. Потолок — у каждой стены свой, по плану потолков (ПТ2); ступени — зоной, кромка короба перед нишей — тонкой линией; в поле потолка: ПТ1 +2,500.
9. Часть марок не уместилась у знаков: коды, высоты и привязки этих позиций — в ведомости точек и выводов под видами.

Допущения и предложения на листе. Знак «*» принято (замерить): окно пом. 1 (стена А), дверь пом. 1 (стена В). Знак «**» предложено (согласовать). См. лист открытых вопросов (листы 6, 7).

1000 мм · печать 1:1

Изм.	Кол.уч	Лист	№ док.	Подп.	Дата
Разраб.		Кырлан А.С.			13.11.26
Пров.					
ГИП					
Н. контр.					
Утв.					

ГД-2026-011-АИ

Квартира 56 м²

ЖК «Северный парк», Москва

Дизайн-проект интерьера

Стадия	Лист	Листов
РП	84	119

Развёртка стены Г. Гостиная-кухня (пом. 1), кухонный фронт

М 1:20

Кырлан Александр Сергеевич


выпуск 13.11.2026 № eb7810814f · стр. 93 из 139

Развёртка стены А. Гостиная-кухня (пом. 1)

Гостиная-кухня (пом. 1) · вид изнутри помещения · размеры в мм, отметки в м

ПРЕДВАРИТЕЛЬНО · не для производства работ · открыто пунктов: 13 (реестр — л. 6, 7)

Стена А (М 1:25)

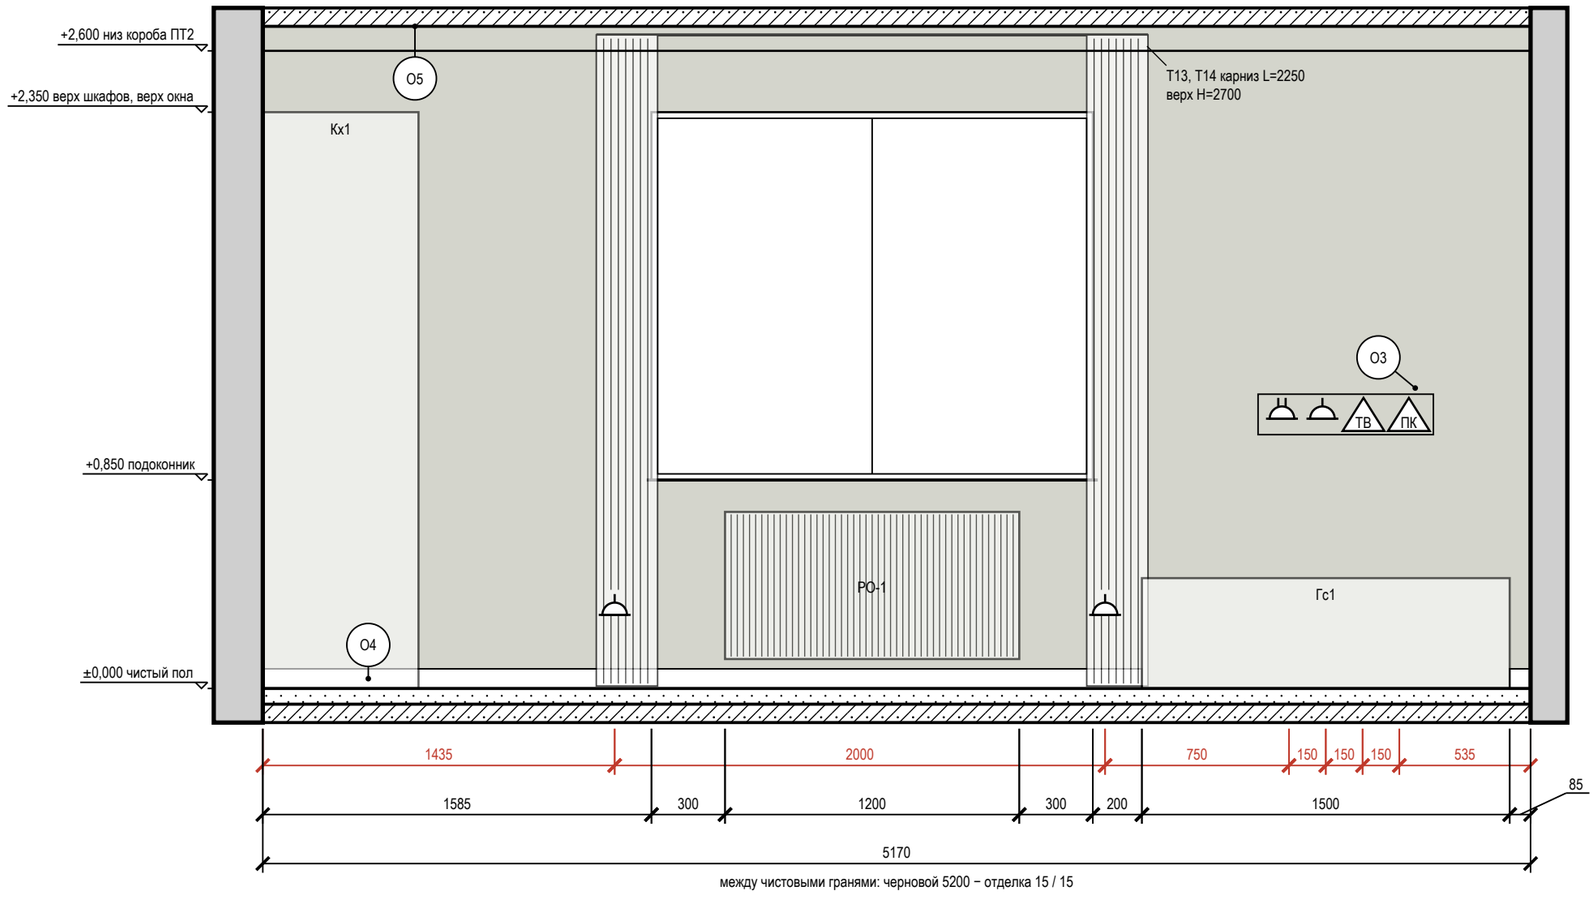

между чистовыми гранями: черновой 5200 − отделка 15 / 15

Ведомость точек и выводов

Марка	Что это	Гр.	H, мм	От угла, мм	Примечание
Р24	розетка: у обеденного стола	6	300	1435	
Р20	розетка: у ТВ-тумбы	6	300	3435	
Р18**	розетка: ТВ (в одной зоне с ТВ1, LAN3)	6	1100	4185	рамка 2 поста
Р19**	розетка: ТВ-приставка (в одной зоне с ТВ1, LAN3)	6	1100	4335	
ТВ1	розетка ТВ: ТВ-зона		1100	4485	
LAN3	розетка RJ45: Smart TV		1100	4635	

Условные обозначения

- розетка с заземляющим контактом; у знака — марка, ×N постов в рамке, гр. — группа щита, H — высота оси, мм
- ПК — розетка компьютерная RJ45
- ТВ — розетка телевизионная
- привязки точек и выводов от угла и от пола, мм
- мебель и приборы — фасад по расстановке (условно)
- карниз (шина) и шторы в собранном виде: марка T, длина L, верх H
- окно: проём, рама, подоконник
- радиатор отопления; марка — по плану отопления
- стены и перекрытия в сечении
- окраска: тон — цвет по коду производителя (условно)
- О1 — марка отделки по реестру отделки альбома
- А — марка развёртки: буква стены, стрелка — взгляд

Ведомость отделки (на листе)

Марка	Поверхность	Материал, изделие	Цвет, код	Кол.
О3	акцентная стена	окраска, Farrow & Ball Modern Emulsion, матовая, подготовка Q3	Farrow & Ball No. 298 «Bancha»	11,3 м²
О4	плинтус	плинтус МДФ, h 80 мм, аналог: плинтус МДФ под покраску 80×16	NCS S 0804-Y30R «S 0804-Y30R»	3,7 м
О5	потолок	окраска, Tikkurila Euro Power 7, глубокоматовая, подготовка Q3	Tikkurila F485 «Damask»	20,8 м²

Примечания

1. Развёртки — вид на стену изнутри помещения, по часовой стрелке; расположение — на листе 83; размеры — в мм по чистовым поверхностям; отметки — в м от ±0,000; высоты H — от чистого пола помещения до оси изделия, у декора — до центра.
2. Красная цепочка — привязки электроточек и выводов по осям от угла чистовых стен; высота H — у знака, от чистого пола до оси; высоты мебели, проёмов и границ отделки — колонкой отметок слева. У знака — короткая марка; назначение, группа щита, высота и привязка каждой точки и вывода — в «Ведомости точек и выводов» под видами (каждая точка — строка).
3. У знака электроточки: марка (Р — розетка, S — выключатель, Св — светильник, ЭВ — вывод кабеля), ×N — число постов в рамке, гр. — группа щита, H — высота оси от чистого пола, мм; группы по клавишам выключателя — на листе выключателей.
4. Схема мебели, приборов и декора не является технической документацией для производства мебели; габариты — по паспортам изделий.
5. Карнизы (шины) — по ведомости текстиля декоратора: длина L и верх H на развёртке — те же числа, что в ведомости; крепление — до окраски потолка.
6. Потолок — у каждой стены свой, по плану потолков (НШ1, ПТ2); ступени — зоной, кромка короба перед нишей — тонкой линией; в поле потолка: ПТ1 +2,500.
7. Линии узора (швы плитки, складки штор, рёбра радиаторов) прерываются у знаков и выносок — просвет между линиями не менее 0,7 мм.
8. Часть марок не уместилась у знаков: коды, высоты и привязки этих позиций — в ведомости точек и выводов под видами.

Допущения и предложения на листе

Основа листа: размеры помещений и положение проёмов введены заказчиком в брифе, на объекте не замерены (К-1); высота потолка 2700 мм — по брифу заказчика, не замерена (К-2); толщины стен приняты по брифу: наружные 200 мм, внутренние 150 мм — не обмерены (К-1); тип дома монолитный, перекрытие 200 мм — по брифу заказчика, документов нет (К-3); планировка (стены, проёмы, объединение кухни и гостиной, расширение санузла) — по брифу без обмера и плана БТИ (К-7); разрешённая мощность 10 кВт принята, ТУ не переданы (К-8); вентканалы приняты, в брифе не заданы (К-9); подрайон климата не задан — принят не северный (жилые от 2,5 м) (К-10).

Знак «*» — принято, не замерено и не подтверждено (замерить на объекте): К-1: окно пом. 1 (стена А) — окно: положение, ширина, высота и подоконник — по брифу заказчика, не замерены; ограждение 900 мм — предложение исполнителя; дверь пом. 1 (стена В) — Петли у правого откоса (х 4600): открытое полотно стоит у стены Б, вошедший идёт влево к кухне; при петлях слева полотно запирало вход в карман между собой, диваном Гс2 и стеной Б.

Знак «**» — предложение проектировщика, заказчиком не утверждено (согласовать с заказчиком): Р18 — высота 1100 мм выше нормы 1 м (ПУЭ 6.6.30) по назначению: питание ТВ, в одной зоне с выводами ТВ1 и LAN3; Р19 — высота 1100 мм выше нормы 1 м (ПУЭ 6.6.30) по назначению: питание приставки ТВ, в одной зоне с выводами ТВ1 и LAN3.

См. лист открытых вопросов (лист 6, записи К-1–К-3, К-7–К-10).

1000 мм · печать 1:1

Изм.	Кол.уч	Лист	№ док.	Подп.	Дата
Разраб.		Кырлан А.С.			13.11.26
Пров.					
ГИП					
Н. контр.					
Утв.					

ГД-2026-011-АИ

Квартира 56 м²

ЖК «Северный парк», Москва

Дизайн-проект интерьера

Стадия	Лист	Листов
РП	85	119

Развёртка стены А. Гостиная-кухня (пом. 1)

М 1:25

Кырлан Александр Сергеевич


выпуск 13.11.2026 № eb78108814f · стр. 94 из 139

Развёртка стены Б. Гостиная-кухня (пом. 1)

Гостиная-кухня (пом. 1) · вид изнутри помещения · размеры в мм, отметки в м

ПРЕДВАРИТЕЛЬНО · не для производства работ · открыто пунктов: 13 (реестр — л. 6, 7)

Стена Б (М 1:20)

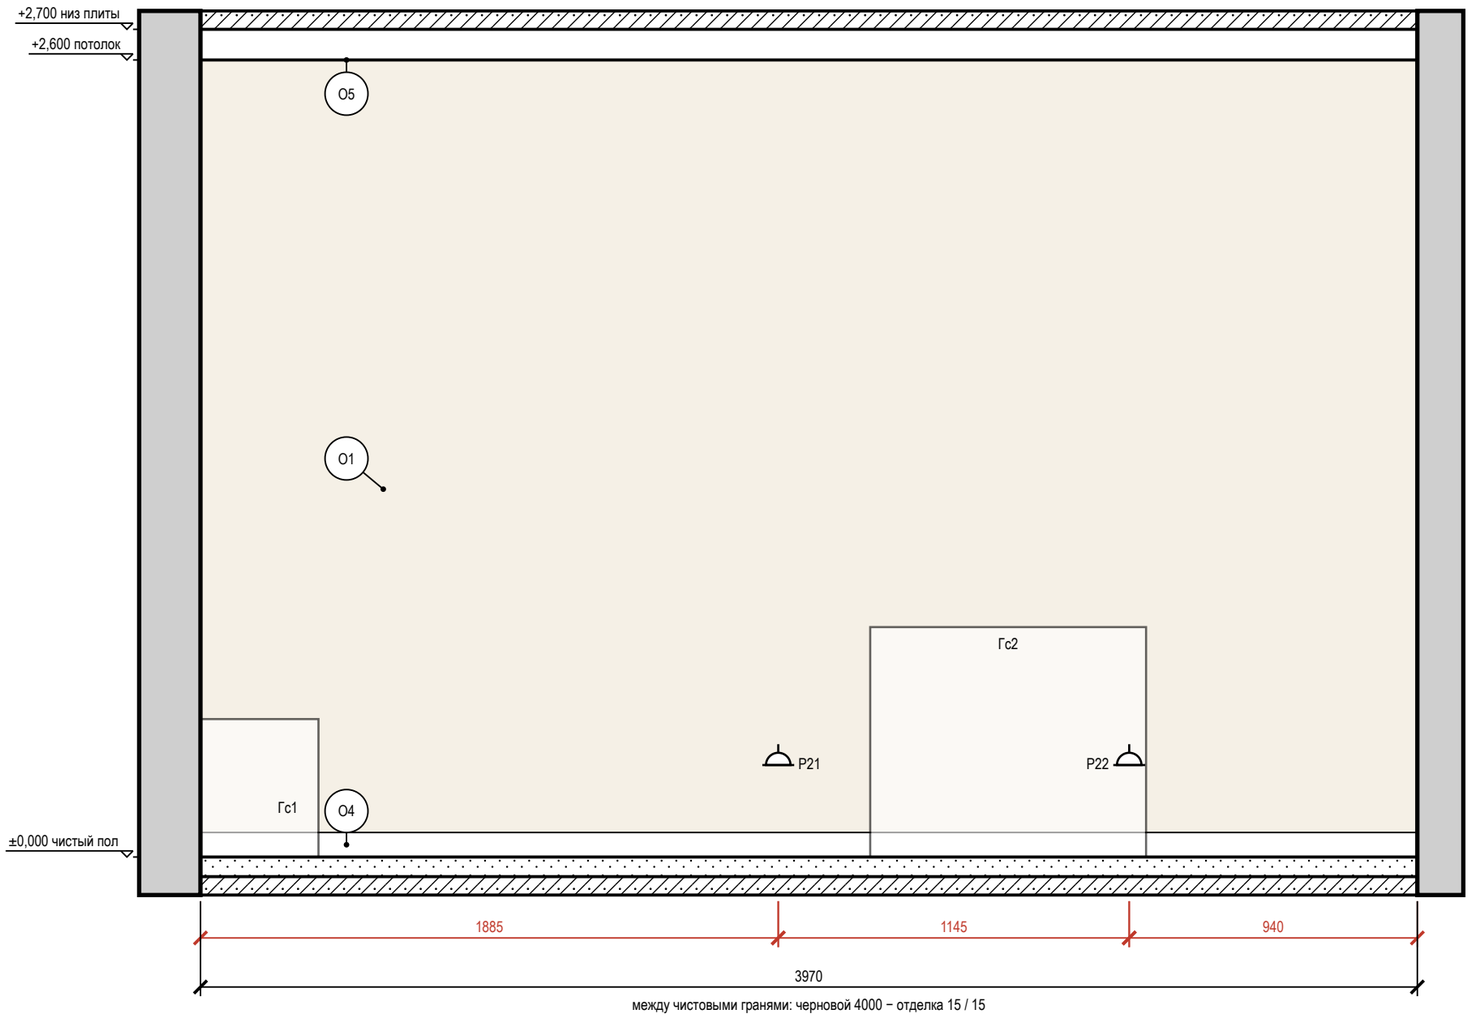

между чистовыми гранями: черновой 4000 − отделка 15 / 15

Ведомость точек и выводов

Марка	Что это	Гр.	Н, мм	От угла, мм	Примечание
Р21	розетка: торшер	6	300	1885	
Р22	розетка: у дивана	6	300	3030	


Условные обозначения

- розетка с заземляющим контактом; у знака — марка, ×N постов в рамке, гр. — группа щита, Н — высота оси, мм
- привязки точек и выводов от угла и от пола, мм
- мебель и приборы — фасад по расстановке (условно)
- стены и перекрытия в сечении
- окраска: тон — цвет по коду производителя (условно)
- О1 — марка отделки по реестру отделки альбома
- А — марка развёртки: буква стены, стрелка — взгляд

Ведомость отделки (на листе)

Марка	Поверхность	Материал, изделие	Цвет, код	Кол.
О1	стены	окраска, Tikkurila Euro Power 7, колеровка по NCS, матовая, подготовка Q3	NCS S 0804-Y30R «S 0804-Y30R»	10,3 м²
О4	плинтус	плинтус МДФ, h 80 мм, аналог: плинтус МДФ под покраску 80×16	NCS S 0804-Y30R «S 0804-Y30R»	4 м
О5	потолок	окраска, Tikkurila Euro Power 7, глубокоматовая, подготовка Q3	Tikkurila F485 «Damask»	20,8 м²

Схема развёрток (М 1:100)

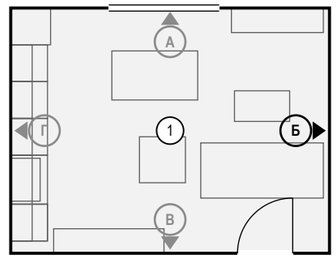

Примечания

1. Развёртки — вид на стену изнутри помещения, по часовой стрелке; расположение — на схеме листа и на листе 83; размеры — в мм по чистовым поверхностям; отметки — в м от ±0,000; высоты Н — от чистого пола помещения до оси изделия, у декора — до центра.
2. Красная цепочка — привязки электроточек и выводов по осям от угла чистовых стен; высота Н — у знака, от чистого пола до оси; высоты мебели, проёмов и границ отделки — колонкой отметок слева. У знака — короткая марка; назначение, группа щита, высота и привязка каждой точки и вывода — в «Ведомости точек и выводов» под видами (каждая точка — строка).
3. У знака электроточки: марка (Р — розетка, S — выключатель, Св — светильник, ЭВ — вывод кабеля), ×N — число постов в рамке, гр. — группа щита, Н — высота оси от чистого пола, мм; группы по клавишам выключателя — на листе выключателей.
4. Схема мебели, приборов и декора не является технической документацией для производства мебели; габариты — по паспортам изделий.
5. Потолок — у каждой стены свой, по плану потолков (ПТ2); ступени — зоной, кромка короба перед нишей — тонкой линией; в поле потолка: ПТ1 +2,500.

Допущения и предложения на листе. Основа листа: размеры помещений и положение проёмов введены заказчиком в брифе, на объекте не замерены (К-1); высота потолка 2700 мм — по брифу заказчика, не замерена (К-2); толщины стен приняты по брифу: наружные 200 мм, внутренние 150 мм — не обмерены (К-1); тип дома монолитный, перекрытие 200 мм — по брифу заказчика, документов нет (К-3); планировка (стены, проёмы, объединение кухни и гостиной, расширение санузла) — по брифу без обмера и плана БТИ (К-7); разрешённая мощность 10 кВт принята, ТУ не переданы (К-8); вентканалы приняты, в брифе не заданы (К-9); подрайон климата не задан — принят не северный (жилые от 2,5 м) (К-10). Знак «*» — принято, не замерено и не подтверждено (замерить на объекте): К-1: окно пом. 1 (стена А) — окно: положение, ширина, высота и подоконник — по брифу заказчика, не замерены; ограждение 900 мм — предложение исполнителя; дверь пом. 1 (стена В) — Петли у правого откоса (х 4600): открытое полотно стоит у стены Б, вошедший идёт влево к кухне; при петлях слева полотно запирало вход в карман между собой, диваном Гс2 и стеной Б. См. лист открытых вопросов (лист 6, записи К-1–К-3, К-7–К-10).

1000 мм · печать 1:1

Изм.	Кол.уч	Лист	№ док.	Подп.	Дата
Разраб.		Кырлан А.С.			13.11.26
Пров.					
ГИП					
Н. контр.					
Утв.					

ГД-2026-011-АИ

Квартира 56 м²

ЖК «Северный парк», Москва

Дизайн-проект интерьера

Стадия	Лист	Листов
РП	86	119

Развёртка стены Б. Гостиная-кухня (пом. 1)

М 1:20

Кырлан Александр Сергеевич


выпуск 13.11.2026 № eb7810814f · стр. 95 из 139

Развёртка стены В. Гостиная-кухня (пом. 1)

Гостиная-кухня (пом. 1) · вид изнутри помещения · размеры в мм, отметки в м

ПРЕДВАРИТЕЛЬНО · не для производства работ · открыто пунктов: 13 (реестр — л. 6, 7)

Стена В (М 1:25)

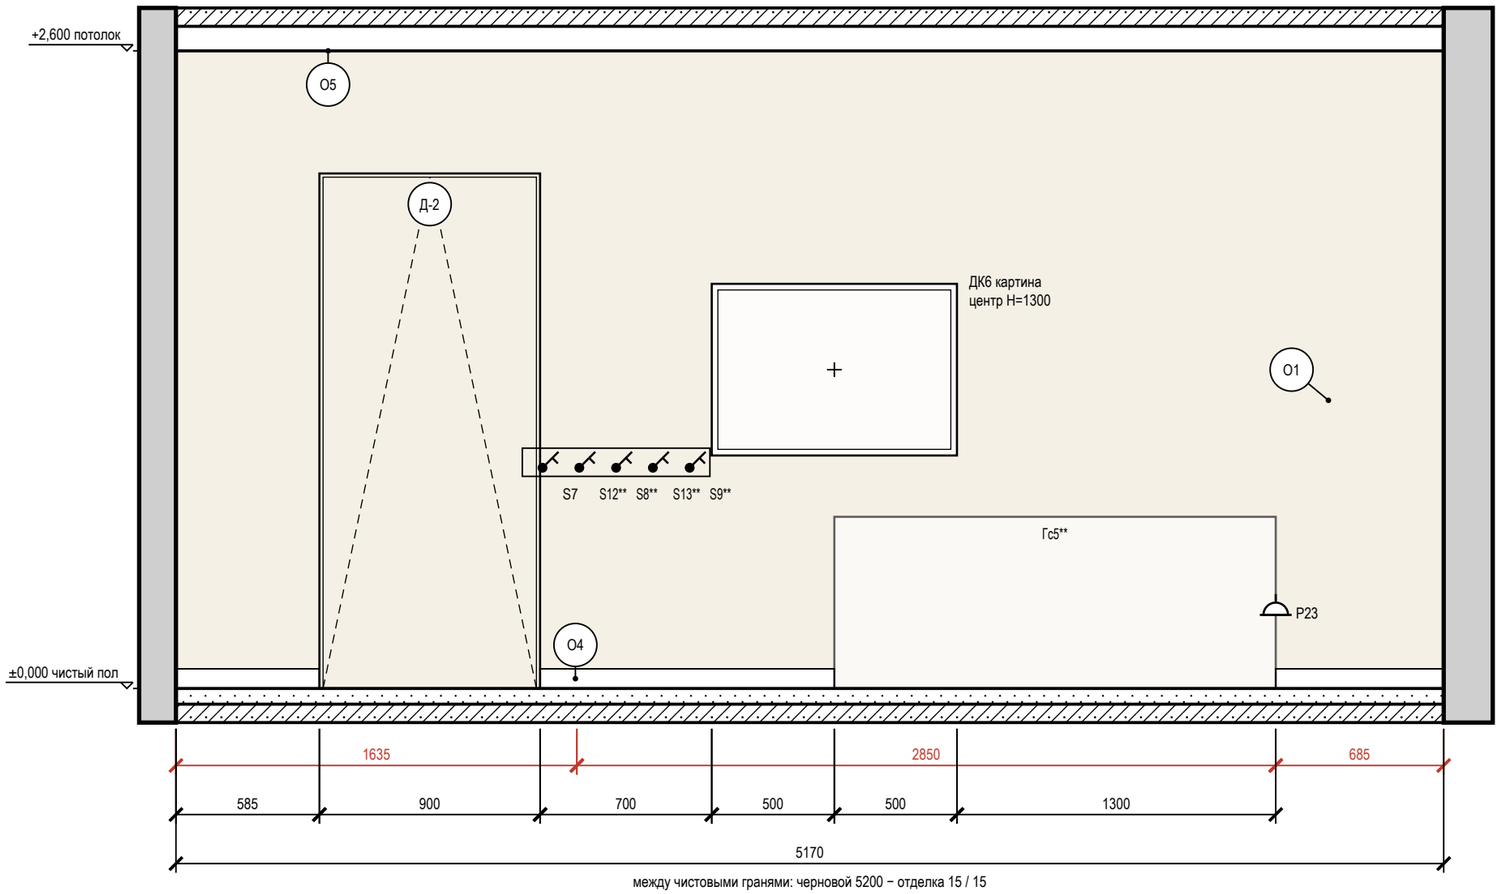

между чистовыми гранями: черновой 5200 − отделка 15 / 15

Ведомость точек и выводов

Марка	Что это	Гр.	Н, мм	От угла, мм	Примечание
S7	выключатель	2	900	1635	
S12**	выключатель	2	900	1715	
S8**	выключатель	2	900	1795	
S13**	выключатель	2	900	1875	
S9**	выключатель	2	900	1955	
Р23	розетка: уборка, пылесос	6	300	4485	

Условные обозначения

- розетка с заземляющим контактом; у знака — марка, ×N постов в рамке, гр. — группа щита, Н — высота оси, мм
- выключатель одноклавишный
- привязки точек и выводов от угла и от пола, мм
- мебель и приборы — фасад по расстановке (условно)
- картина (декор): марка Д, крест — центр, Н — высота центра, мм
- дверь скрытого монтажа: полотно в плоскости стены (узел — на листе узлов)
- стены и перекрытия в сечении
- окраска: тон — цвет по коду производителя (условно)
- О1 — марка отделки по реестру отделки альбома
- А — марка развёртки: буква стены, стрелка — взгляд

Ведомость отделки (на листе)

Марка	Поверхность	Материал, изделие	Цвет, код	Кол.
О1	стены	окраска, Tikkurila Euro Power 7, колеровка по NCS, матовая, подготовка Q3	NCS S 0804-Y30R «S 0804-Y30R»	11,6 м²
О4	плинтус	плинтус МДФ, h 80 мм, аналог: плинтус МДФ под покраску 80×16	NCS S 0804-Y30R «S 0804-Y30R»	2,5 м
О5	потолок	окраска, Tikkurila Euro Power 7, глубокоматовая, подготовка Q3	Tikkurila F485 «Damask»	20,8 м²

Примечания

1. Развёртки — вид на стену изнутри помещения, по часовой стрелке; расположение — на листе 83; размеры — в мм по чистовым поверхностям; отметки — в м от ±0,000; высоты Н — от чистого пола помещения до оси изделия, у декора — до центра.
2. Красная цепочка — привязки электроточек и выводов по осям от угла чистовых стен; высота Н — у знака, от чистого пола до оси; высоты мебели, проёмов и границ отделки — колонкой отметок слева. У знака — короткая марка; назначение, группа щита, высота и привязка каждой точки и вывода — в «Ведомости точек и выводов» под видами (каждая точка — строка).
3. У знака электроточки: марка (Р — розетка, S — выключатель, Св — светильник, ЭВ — вывод кабеля), ×N — число постов в рамке, гр. — группа щита, Н — высота оси от чистого пола, мм; группы по клавишам выключателя — на листе выключателей.
4. Схема мебели, приборов и декора не является технической документацией для производства мебели; габариты — по паспортам изделий.
5. Картины и зеркала крепить к основанию по паспорту изделия (закладные и анкеры — в перечне скрытых работ); крест — ось центра предмета.
6. Двери скрытого монтажа — полотно в плоскости стены, отделка стены по полотну, плинтус прерывается у короба (узел — на листе узлов).
7. Потолок — у каждой стены свой, по плану потолков (ПТ2); ступени — зоной, кромка короба перед нишей — тонкой линией; в поле потолка: ПТ1 +2,500.

Допущения и предложения на листе. Основа листа: размеры помещений и положение проёмов введены заказчиком в брифе, на объекте не замерены (К-1); высота потолка 2700 мм — по брифу заказчика, не замерена (К-2); толщины стен приняты по брифу: наружные 200 мм, внутренние 150 мм — не обмерены (К-1); тип дома монолитный, перекрытие 200 мм — по брифу заказчика, документов нет (К-3); планировка (стены, проёмы, объединение кухни и гостиной, расширение санузла) — по брифу без обмера и плана БТИ (К-7); разрешённая мощность 10 кВт принята, ТУ не переданы (К-8); вентканалы приняты, в брифе не заданы (К-9); подрайон климата не задан — принят не северный (жилые от 2,5 м) (К-10). Знак «*» — принято, не замерено и не подтверждено (замерить на объекте): К-1: окно пом. 1 (стена А) — окно: положение, ширина, высота и подоконник — по брифу заказчика, не замерены; ограждение 900 мм — предложение исполнителя; дверь пом. 1 (стена В) — Петли у правого откоса (х 4600): открытое полотно стоит у стены Б, вошедший идёт влево к кухне; при петлях слева полотно запирало вход в карман между собой, диваном Гс2 и стеной Б. Знак «**» — предложение проектировщика, заказчиком не утверждено (согласовать с заказчиком): S12 — свой пост группе L13: сценарии «Вечер», «Ужин», «Кино», «Готовка» включают её отдельно от L12 — на одном светорегуляторе не набрать; S8, S9 — светорегулятор добавлен разработчиком проекта; S13 — свой пост группе L15: сценарии «Вечер», «Ужин», «Готовка» включают её отдельно от L14 — на одном светорегуляторе не набрать; ИЗ-1, ИЗ-3: Гс5 — Было смещение 1600…3400 у двери Д-2 (3700…4600): между консолью и креслом/диваном оставался проход 575–625 мм, из двери к кухне не пройти. См. лист открытых вопросов (лист 6, записи К-1–К-3, К-7–К-10; лист 7, записи ИЗ-1, ИЗ-3).

1000 мм · печать 1:1

Изм.	Кол.уч	Лист	№ док.	Подп.	Дата
Разраб.		Кырлан А.С.			13.11.26
Пров.					
ГИП					
Н. контр.					
Утв.					

ГД-2026-011-АИ

Квартира 56 м²

ЖК «Северный парк», Москва

Дизайн-проект интерьера

Стадия	Лист	Листов
РП	87	119

Развёртка стены В. Гостиная-кухня (пом. 1)

М 1:25

Кырлан Александр Сергеевич


выпуск 13.11.2026 № eb7810814f · стр. 96 из 139

Развёртка стены А. Спальня (пом. 2)

Спальня (пом. 2) · вид изнутри помещения · размеры в мм, отметки в м

ПРЕДВАРИТЕЛЬНО · не для производства работ · открыто пунктов: 13 (реестр — л. 6, 7)

Стена А (М 1:20)

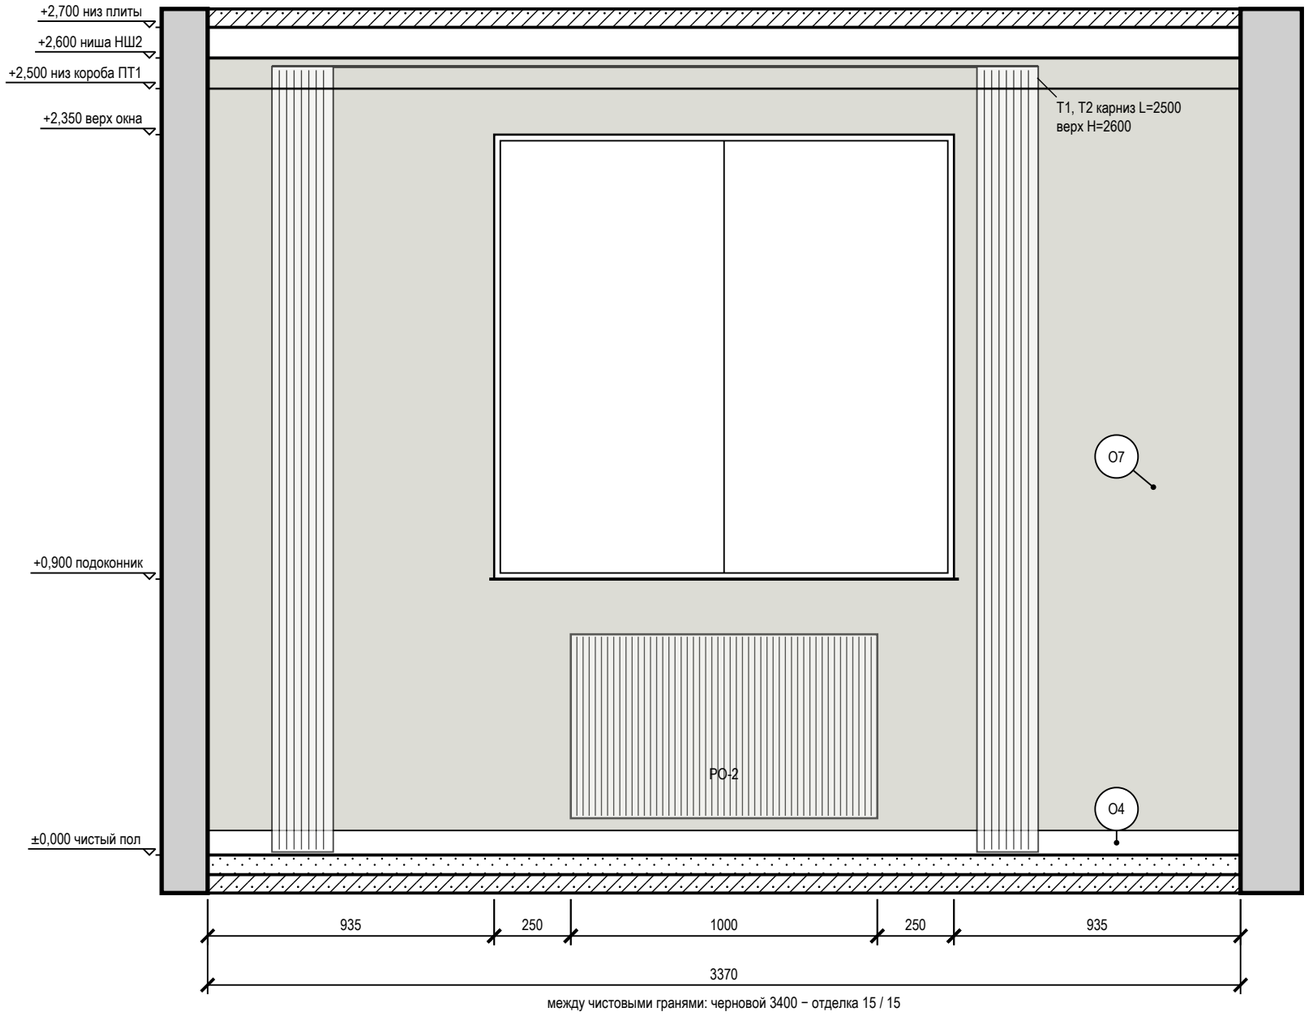

между чистовыми гранями: черновой 3400 − отделка 15 / 15


Условные обозначения

- мебель и приборы — фасад по расстановке (условно)
- карниз (шина) и шторы в собранном виде: марка T, длина L, верх H
- окно: проём, рама, подоконник
- радиатор отопления; марка — по плану отопления
- стены и перекрытия в сечении
- окраска: тон — цвет по коду производителя (условно)
- О1 — марка отделки по реестру отделки альбома
- А — марка развёртки: буква стены, стрелка взгляд

Ведомость отделки (на листе)

Марка	Поверхность	Материал, изделие	Цвет, код	Кол.
О4	плинтус	плинтус МДФ, h 80 мм, аналог: плинтус МДФ под покраску 80×16	NCS S 0804-Y30R «S 0804-Y30R»	3,4 м
О5	потолок	окраска, Tikkurila Euro Power 7, глубокоматовая, подготовка Q3	Tikkurila F485 «Damask»	13,6 м²
О7	акцентная стена	окраска, Tikkurila Euro Power 7, колеровка по NCS, матовая, подготовка Q3	NCS S 5010-G70Y «S 5010-G70Y»	6,6 м²

Схема развёрток (М 1:50)

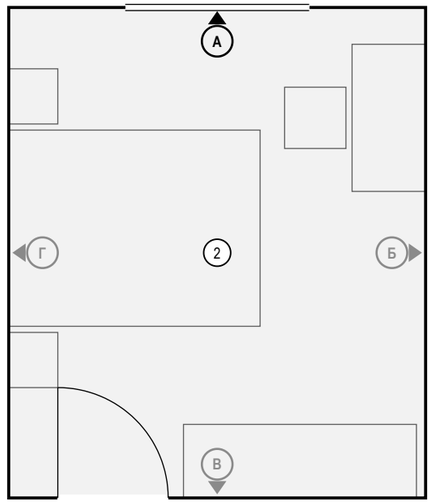

Ведомость изделий и проёмов (на листе)

Марка	Изделие, проём	На виде Ш×В, мм	Низ, мм
РО-2	радиатор отопления	1000×600	120

Примечания

1. Развёртки — вид на стену изнутри помещения, по часовой стрелке; расположение — на схеме листа и на листе 83; размеры — в мм по чистовым поверхностям; отметки — в м от ±0,000; высоты H — от чистого пола помещения до оси изделия, у декора — до центра.
2. Схема мебели, приборов и декора не является технической документацией для производства мебели; габариты — по паспортам изделий.
3. Карнизы (шины) — по ведомости текстиля декоратора: длина L и верх H на развёртке — те же числа, что в ведомости; крепление — до окраски потолка.
4. Потолок — у каждой стены свой, по плану потолков (НШ2, ПТ1); ступени — зоной, кромка короба перед нишей — тонкой линией; в поле потолка: ПТ2 +2,600.

Допущения и предложения на листе

Основа листа: размеры помещений и положение проёмов введены заказчиком в брифе, на объекте не замерены (К-1); высота потолка 2700 мм — по брифу заказчика, не замерена (К-2); толщины стен приняты по брифу: наружные 200 мм, внутренние 150 мм — не обмерены (К-1); тип дома монолитный, перекрытие 200 мм — по брифу заказчика, документов нет (К-3); планировка (стены, проёмы, объединение кухни и гостиной, расширение санузла) — по брифу без обмера и плана БТИ (К-7); разрешённая мощность 10 кВт принята, ТУ не переданы (К-8); вентканалы приняты, в брифе не заданы (К-9); подрайон климата не задан — принят не северный (жилые от 2,5 м) (К-10).
Знак «*» — принято, не замерено и не подтверждено (замерить на объекте): К-1: окно пом. 2 (стена А) — окно: положение, ширина, высота и подоконник — по брифу заказчика, не замерены; дверь пом. 2 (стена В) — проём в существующей стене между пом. 2 и 5: положение и ширина — по брифу заказчика, не замерены.
См. лист открытых вопросов (лист 6, записи К-1–К-3, К-7–К-10).

1000 мм · печать 1:1

Изм.	Кол.уч	Лист	№ док.	Подп.	Дата
Разраб.		Кырлан А.С.			13.11.26
Пров.					
ГИП					
Н. контр.					
Утв.					

ГД-2026-011-АИ

Квартира 56 м²

ЖК «Северный парк», Москва

Дизайн-проект интерьера

Стадия	Лист	Листов
РП	88	119

Развёртка стены А. Спальня (пом. 2)

М 1:20

Кырлан Александр Сергеевич


выпуск 13.11.2026 № eb7810814f · стр. 97 из 139

Развёртка стены Б. Спальня (пом. 2)

Спальня (пом. 2) · вид изнутри помещения · размеры в мм, отметки в м

ПРЕДВАРИТЕЛЬНО · не для производства работ · открыто пунктов: 13 (реестр — л. 6, 7)

Стена Б (М 1:20)

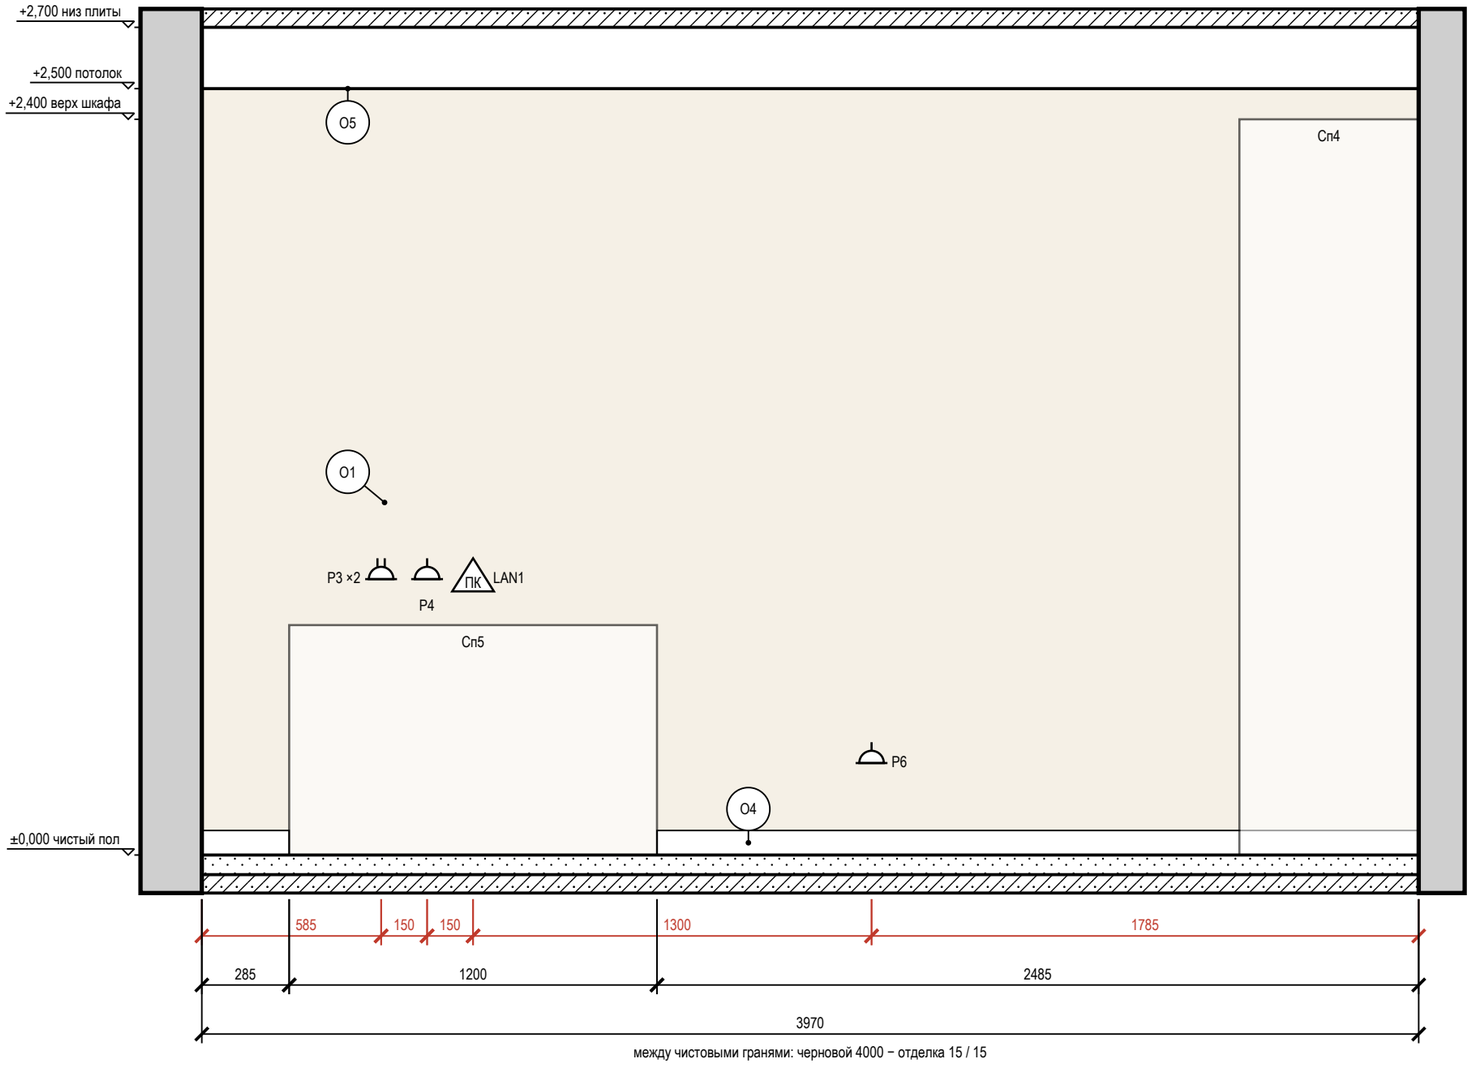

Ведомость точек и выводов

Марка	Что это	Гр.	Н, мм	От угла, мм	Примечание
Р3	розетка: рабочий стол	4	900	585	рамка 2 поста
Р4	розетка: рабочий стол	4	900	735	
LAN1	розетка RJ45: рабочий стол		900	885	
Р6	розетка: уборка	4	300	2185	


Условные обозначения

- розетка с заземляющим контактом; у знака марка, ×N — постов в рамке, гр. — группа щита, Н — высота оси, мм
- ПК — розетка компьютерная RJ45
- привязки точек и выводов от угла и от пола, мм
- мебель и приборы — фасад по расстановке (условно)
- стены и перекрытия в сечении
- окраска: тон — цвет по коду производителя (условно)
- О1 — марка отделки по реестру отделки альбома
- А — марка развёртки: буква стены, стрелка взгляд

Ведомость отделки (на листе)

Марка	Поверхность	Материал, изделие	Цвет, код	Кол.
О1	стены	окраска, Tikkurila Euro Power 7, колеровка по NCS, матовая, подготовка Q3	NCS S 0804-Y30R «S 0804-Y30R»	9,9 м²
О4	плинтус	плинтус МДФ, h 80 мм, аналог: плинтус МДФ под покраску 80×16	NCS S 0804-Y30R «S 0804-Y30R»	2,8 м
О5	потолок	окраска, Tikkurila Euro Power 7, глубокоматовая, подготовка Q3	Tikkurila F485 «Damask»	13,6 м²

Схема развёрток (М 1:100)

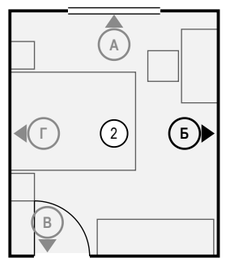

Примечания

1. Развёртки — вид на стену изнутри помещения, по часовой стрелке; расположение — на схеме листа и на листе 83; размеры — в мм по чистовым поверхностям; отметки — в м от ±0,000; высоты Н — от чистого пола помещения до оси изделия, у декора — до центра.
2. Красная цепочка — привязки электроточек и выводов по осям от угла чистовых стен; высота Н — у знака, от чистого пола до оси; высоты мебели, проёмов и границ отделки — колонкой отметок слева. У знака — короткая марка; назначение, группа щита, высота и привязка каждой точки и вывода — в «Ведомости точек и выводов» под видами (каждая точка — строка).
3. У знака электроточки: марка (Р — розетка, S — выключатель, Св — светильник, ЭВ — вывод кабеля), ×N — число постов в рамке, гр. — группа щита, Н — высота оси от чистого пола, мм; группы по клавишам выключателя — на листе выключателей.
4. Схема мебели, приборов и декора не является технической документацией для производства мебели; габариты — по паспортам изделий.
5. Потолок — у каждой стены свой, по плану потолков (ПТ1); ступени — зоной, кромка короба перед нишей — тонкой линией; в поле потолка: ПТ2 +2,600.

Допущения и предложения на листе

Основа листа: размеры помещений и положение проёмов введены заказчиком в брифе, на объекте не замерены (К-1); высота потолка 2700 мм — по брифу заказчика, не замерена (К-2); толщины стен приняты по брифу: наружные 200 мм, внутренние 150 мм — не обмерены (К-1); тип дома монолитный, перекрытие 200 мм — по брифу заказчика, документов нет (К-3); планировка (стены, проёмы, объединение кухни и гостиной, расширение санузла) — по брифу без обмера и плана БТИ (К-7); разрешённая мощность 10 кВт принята, ТУ не переданы (К-8); вентканалы приняты, в брифе не заданы (К-9); подрайон климата не задан — принят не северный (жилые от 2,5 м) (К-10).

Знак «*» — принято, не замерено и не подтверждено (замерить на объекте): К-1: окно пом. 2 (стена А) — окно: положение, ширина, высота и подоконник — по брифу заказчика, не замерены; дверь пом. 2 (стена В) — проём в существующей стене между пом. 2 и 5: положение и ширина — по брифу заказчика, не замерены.

См. лист открытых вопросов (лист 6, записи К-1–К-3, К-7–К-10).

1000 мм · печать 1:1

Изм.	Кол.уч	Лист	№ док.	Подп.	Дата
Разраб.		Кырлан А.С.			13.11.26
Пров.					
ГИП					
Н. контр.					
Утв.					

ГД-2026-011-АИ

Квартира 56 м²

ЖК «Северный парк», Москва

Дизайн-проект интерьера

Стадия	Лист	Листов
РП	89	119

Развёртка стены Б. Спальня (пом. 2)

М 1:20

Кырлан Александр Сергеевич


выпуск 13.11.2026 № eb7810814f · стр. 98 из 139

Развёртка стены В. Спальня (пом. 2)

Спальня (пом. 2) · вид изнутри помещения · размеры в мм, отметки в м

ПРЕДВАРИТЕЛЬНО · не для производства работ · открыто пунктов: 13 (реестр — л. 6, 7)

Стена В (М 1:20)

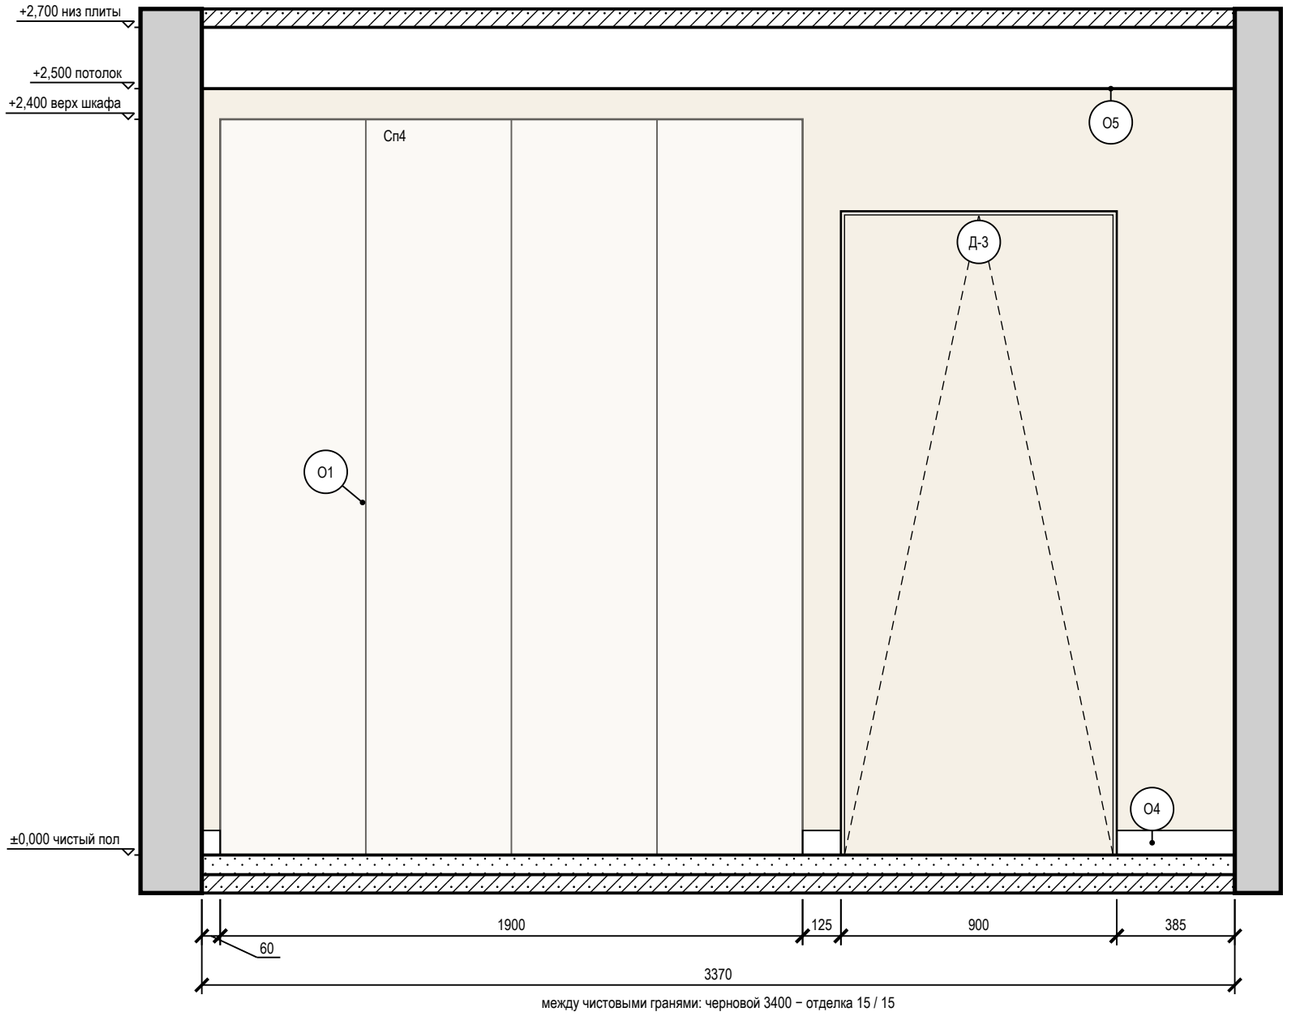

между чистовыми гранями: черновой 3400 − отделка 15 / 15


Условные обозначения

- мебель и приборы — фасад по расстановке (условно)
- дверь скрытого монтажа: полотно в плоскости стены (узел — на листе узлов)
- стены и перекрытия в сечении
- окраска: тон — цвет по коду производителя (условно)
- О1 — марка отделки по реестру отделки альбома
- А — марка развёртки: буква стены, стрелка — взгляд

Ведомость отделки (на листе)

Марка	Поверхность	Материал, изделие	Цвет, код	Кол.
О1	стены	окраска, Tikkurila Euro Power 7, колеровка по NCS, матовая, подготовка Q3	NCS S 0804-Y30R «S 0804-Y30R»	1,8 м²
О4	плинтус	плинтус МДФ, h 80 мм, аналог: плинтус МДФ под покраску 80×16	NCS S 0804-Y30R «S 0804-Y30R»	0,6 м
О5	потолок	окраска, Tikkurila Euro Power 7, глубокоматовая, подготовка Q3	Tikkurila F485 «Damask»	13,6 м²

Схема развёрток (М 1:100)

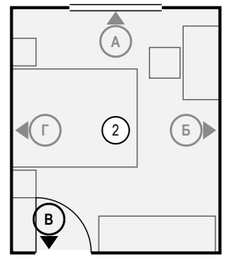

Ведомость изделий и проёмов (на листе)

Марка	Изделие, проём	На виде Ш×В, мм	Низ, мм
Сп4	шкаф распашной 1900×600 до 2400, фасады — дуб рифлёный	1900×2400	0
Д-3	дверь скрытого монтажа	900×2100	0

Примечания

1. Развёртки — вид на стену изнутри помещения, по часовой стрелке; расположение — на схеме листа и на листе 83; размеры — в мм по чистовым поверхностям; отметки — в м от ±0,000; высоты Н — от чистого пола помещения до оси изделия, у декора — до центра.
2. Схема мебели, приборов и декора не является технической документацией для производства мебели; габариты — по паспортам изделий.
3. Двери скрытого монтажа — полотно в плоскости стены, отделка стены по полотну, плинтус прерывается у короба (узел — на листе узлов).
4. Потолок — у каждой стены свой, по плану потолков (ПТ1); ступени — зоной, кромка короба перед нишей — тонкой линией; в поле потолка: ПТ2 +2,600.

Допущения и предложения на листе

Основа листа: размеры помещений и положение проёмов введены заказчиком в брифе, на объекте не замерены (К-1); высота потолка 2700 мм — по брифу заказчика, не замерена (К-2); толщины стен приняты по брифу: наружные 200 мм, внутренние 150 мм — не обмерены (К-1); тип дома монолитный, перекрытие 200 мм — по брифу заказчика, документов нет (К-3); планировка (стены, проёмы, объединение кухни и гостиной, расширение санузла) — по брифу без обмера и плана БТИ (К-7); разрешённая мощность 10 кВт принята, ТУ не переданы (К-8); вентканалы приняты, в брифе не заданы (К-9); подрайон климата не задан — принят не северный (жилые от 2,5 м) (К-10).

Знак «*» — принято, не замерено и не подтверждено (замерить на объекте): К-1: окно пом. 2 (стена А) — окно: положение, ширина, высота и подоконник — по брифу заказчика, не замерены; дверь пом. 2 (стена В) — проём в существующей стене между пом. 2 и 5: положение и ширина — по брифу заказчика, не замерены.

См. лист открытых вопросов (лист 6, записи К-1–К-3, К-7–К-10).

1000 мм · печать 1:1

Изм.	Кол.уч	Лист	№ док.	Подп.	Дата
Разраб.		Кырлан А.С.			13.11.26
Пров.					
ГИП					
Н. контр.					
Утв.					

ГД-2026-011-АИ

Квартира 56 м²

ЖК «Северный парк», Москва

Дизайн-проект интерьера

Стадия	Лист	Листов
РП	90	119

Развёртка стены В. Спальня (пом. 2)

М 1:20

Кырлан Александр Сергеевич


выпуск 13.11.2026 № eb7810814f · стр. 99 из 139

Развёртка стены Г. Спальня (пом. 2)

Спальня (пом. 2) · вид изнутри помещения · размеры в мм, отметки в м

ПРЕДВАРИТЕЛЬНО · не для производства работ · открыто пунктов: 13 (реестр — л. 6, 7)

Стена Г (М 1:20)

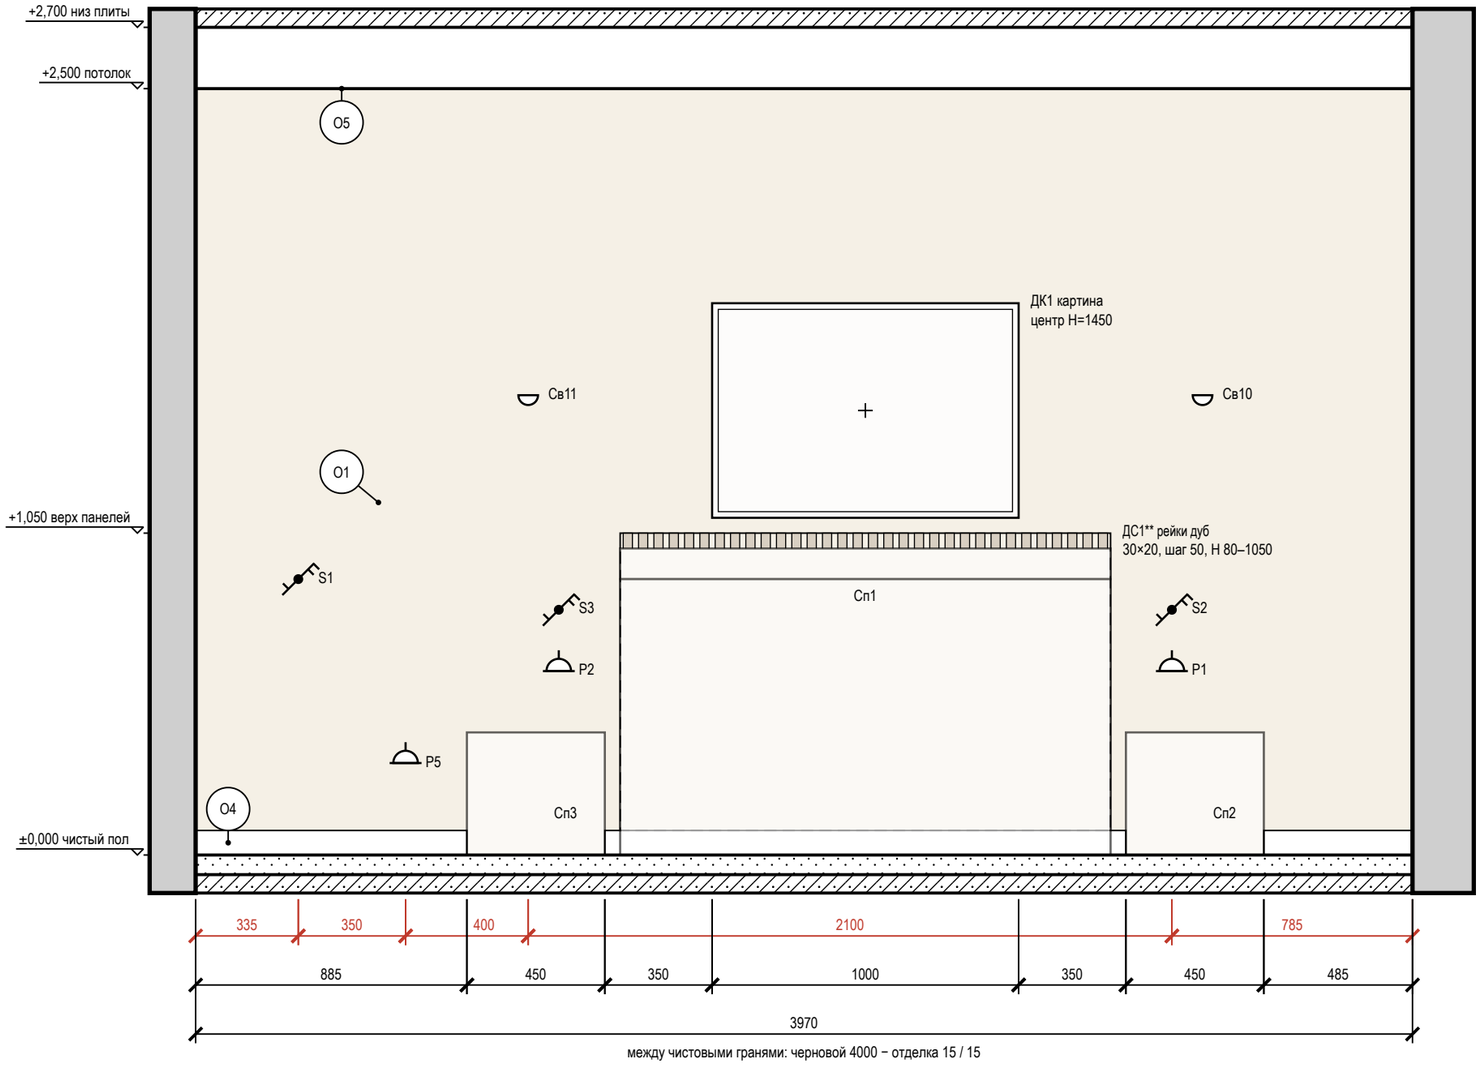


Ведомость точек и выводов

Марка	Что это	Гр.	H, мм	От угла, мм	Примечание
S1	выключатель	1	900	335	
P5	розетка: торшер	4	300	685	
Св11	светильник настенный	1	1500	1085	
P2	розетка: у кровати	4	600	1185	
S3	выключатель	1	800	1185	
P1	розетка: у кровати	4	600	3185	
S2	выключатель	1	800	3185	
Св10	светильник настенный	1	1500	3285	

Условные обозначения

- розетка с заземляющим контактом; у знака марка, ×N — постов в рамке, гр. — группа щита, H — высота оси, мм
- выключатель одноклавишный
- выключатель двухклавишный (флажков — по числу клавиш)
- выключатель с проходной или перекрёстной клавишей (обратный флажок); тип клавиши — в подписи
- светильник настенный (бра), H — высота оси
- привязки точек и выводов от угла и от пола, мм
- мебель и приборы — фасад по расстановке (условно)
- картина (декор): марка Д, крест — центр, H — высота центра, мм
- стены и перекрытия в сечении
- объёмная отделка стены (панели, рейки, молдинги, плинтус, карниз): марка, материал, сечение, шаг, H от чистого пола, мм
- окраска: тон — цвет по коду производителя (условно)
- О1 — марка отделки по реестру отделки альбома
- А — марка развёртки: буква стены, стрелка взгляд

Схема развёрток (М 1:100)

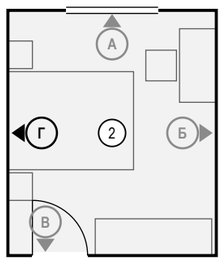

Примечания

1. Развёртки — вид на стену изнутри помещения, по часовой стрелке; расположение — на схеме листа и на листе 83; размеры — в мм по чистовым поверхностям; отметки — в м от ±0,000; высоты H — от чистого пола помещения до оси изделия, у декора — до центра.
2. Красная цепочка — привязки электроточек и выводов по осям от угла чистовых стен; высота H — у знака, от чистого пола до оси; высоты мебели, проёмов и границ отделки — колонкой отметок слева. У знака — короткая марка; назначение, группа щита, высота и привязка каждой точки и вывода — в «Ведомости точек и выводов» под видами (каждая точка — строка).
3. Отделка стен — по ведомости отделки помещений, лист 61.
4. У знака электроточки: марка (P — розетка, S — выключатель, Св — светильник, ЭВ — вывод кабеля), ×N — число постов в рамке, гр. — группа щита, H — высота оси от чистого пола, мм; группы по клавишам выключателя — на листе выключателей.
5. Схема мебели, приборов и декора не является технической документацией для производства мебели; габариты — по паспортам изделий.
6. Картины и зеркала крепить к основанию по паспорту изделия (закладные и анкеры — в перечне скрытых работ); крест — ось центра предмета.
7. Объёмная отделка стен — по ведомости отделки листа: материал, сечение, шаг и отметки — по подписи у элемента; рейки и рамки молдингов раскладываются от середины поля; крепление — по паспорту изделия.
8. Объёмная отделка за мебелью и приборами не показана, граница её поля за ними — штриховой линией.
9. Потолок — у каждой стены свой, по плану потолков (ПТ1); ступени — зоной, кромка короба перед нишей — тонкой линией; в поле потолка: ПТ2 +2,600.

Допущения и предложения на листе. Знак «*» принято (замерить): окно пом. 2 (стена А), дверь пом. 2 (стена В). Знак «**» предложено (согласовать). См. лист открытых вопросов (листы 6, 7).

1000 мм · печать 1:1

Изм.	Кол.уч	Лист	№ док.	Подп.	Дата
Разраб.		Кырлан А.С.			13.11.26
Пров.					
ГИП					
Н. контр.					
Утв.					

ГД-2026-011-АИ

Квартира 56 м²

ЖК «Северный парк», Москва

Дизайн-проект интерьера

Стадия	Лист	Листов
РП	91	119

Развёртка стены Г. Спальня (пом. 2)

М 1:20

Кырлан Александр Сергеевич


выпуск 13.11.2026 № eb7810814f · стр. 100 из 139

Развёртка стены А. Детская (пом. 3)

Детская (пом. 3) · вид изнутри помещения · размеры в мм, отметки в м

ПРЕДВАРИТЕЛЬНО · не для производства работ · открыто пунктов: 13 (реестр — л. 6, 7)

Стена А (М 1:20)

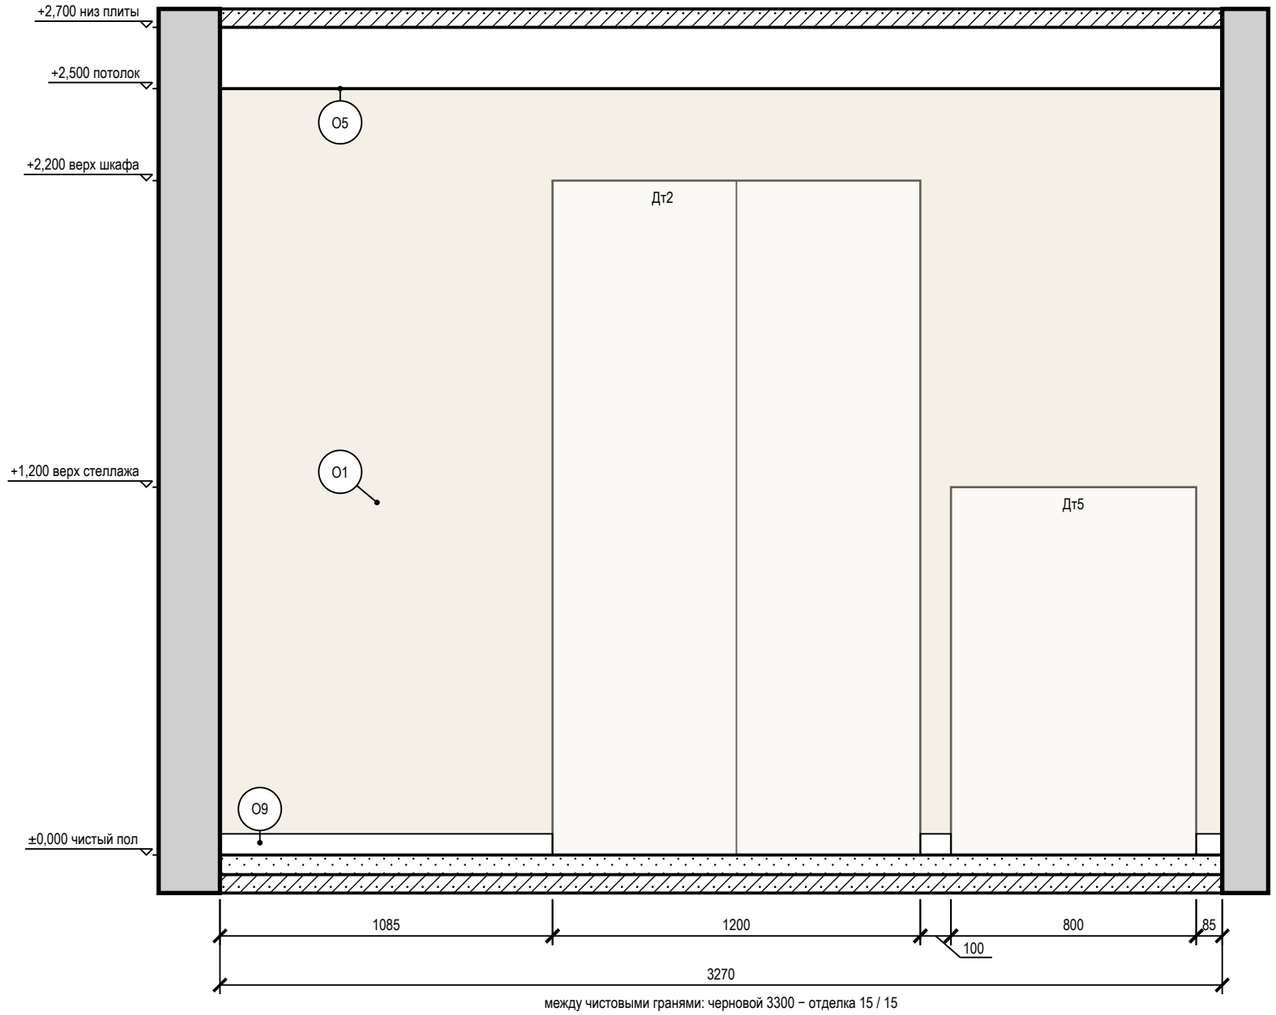


между чистовыми гранями: черновой 3300 − отделка 15 / 15

Ведомость отделки (на листе)

Марка	Поверхность	Материал, изделие	Цвет, код	Кол.
О1	стены	окраска, Tikkurila Euro Power 7, колеровка по NCS, матовая, подготовка Q3	NCS S 0804-Y30R «S 0804-Y30R»	8,2 м²
О5	потолок	окраска, Tikkurila Euro Power 7, глубокоматовая, подготовка Q3	Tikkurila F485 «Damask»	8,6 м²
О9	плинтус	плинтус МДФ, Orac Decor Contour (Luxxus), h 69 мм, SX165	NCS S 0804-Y30R «S 0804-Y30R»	1,3 м

Схема развёрток (М 1:50)

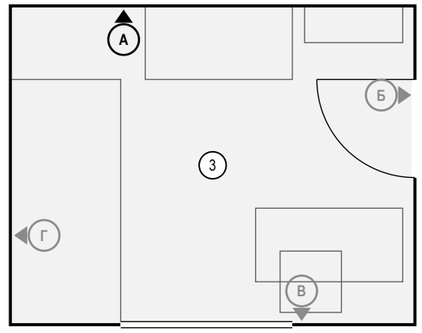

Допущения и предложения на листе

Основа листа: размеры помещений и положение проёмов введены заказчиком в брифе, на объекте не замерены (К-1); высота потолка 2700 мм — по брифу заказчика, не замерена (К-2); толщины стен приняты по брифу: наружные 200 мм, внутренние 150 мм — не обмерены (К-1); тип дома монолитный, перекрытие 200 мм — по брифу заказчика, документов нет (К-3); планировка (стены, проёмы, объединение кухни и гостиной, расширение санузла) — по брифу без обмера и плана БТИ (К-7); разрешённая мощность 10 кВт принята, ТУ не переданы (К-8); вентканалы приняты, в брифе не заданы (К-9); подрайон климата не задан — принят не северный (жилые от 2,5 м) (К-10).

Знак «*» — принято, не замерено и не подтверждено (замерить на объекте): К-1: окно пом. 3 (стена В) — окно: положение, ширина, высота и подоконник — по брифу заказчика, не замерены.

Знак «**» — предложение проектировщика, заказчиком не утверждено (согласовать с заказчиком): К-5: дверь пом. 3 (стена Б) — дверь в новой перегородке: проём по брифу, короб скрытой двери и размер в свету — после выбора модели и утверждения перегородки (К-5).

См. лист открытых вопросов (лист 6, записи К-1–К-3, К-5, К-7–К-10).

Условные обозначения

- мебель и приборы — фасад по расстановке (условно)
- стены и перекрытия в сечении
- окраска: тон — цвет по коду производителя (условно)
- О1 — марка отделки по реестру отделки альбома
- А — марка развёртки: буква стены, стрелка — взгляд

Ведомость изделий и проёмов (на листе)

Марка	Изделие, проём	На виде Ш×В, мм	Низ, мм
Дт2	шкаф 1200×600 до 2200, фасады — дуб и серо-зелёный	1200×2200	0
Дт5	стеллаж низкий для книг и игрушек 800×300	800×1200	0

Примечания

1. Развёртки — вид на стену изнутри помещения, по часовой стрелке; расположение — на схеме листа и на листе 83; размеры — в мм по чистовым поверхностям; отметки — в м от ±0,000; высоты Н — от чистого пола помещения до оси изделия, у декора — до центра.
2. Схема мебели, приборов и декора не является технической документацией для производства мебели; габариты — по паспортам изделий.
3. Потолок — у каждой стены свой, по плану потолков (ПТ1); ступени — зоной, кромка короба перед нишей — тонкой линией; в поле потолка: ПТ2 +2,600.

1000 мм · печать 1:1

Изм.	Кол.уч	Лист	№ док.	Подп.	Дата
Разраб.		Кырлан А.С.			13.11.26
Пров.					
ГИП					
Н. контр.					
Утв.					

ГД-2026-011-АИ

Квартира 56 м²

ЖК «Северный парк», Москва

Дизайн-проект интерьера

Стадия	Лист	Листов
РП	92	119

Развёртка стены А. Детская (пом. 3)

М 1:20

Кырлан Александр Сергеевич


выпуск 13.11.2026 № eb7810814f · стр. 101 из 139

Развёртки стен Б, Г. Детская (пом. 3)

Детская (пом. 3) · вид изнутри помещения · размеры в мм, отметки в м


ПРЕДВАРИТЕЛЬНО · не для производства работ · открыто пунктов: 13 (реестр — л. 6, 7)

Стена Б (М 1:25)

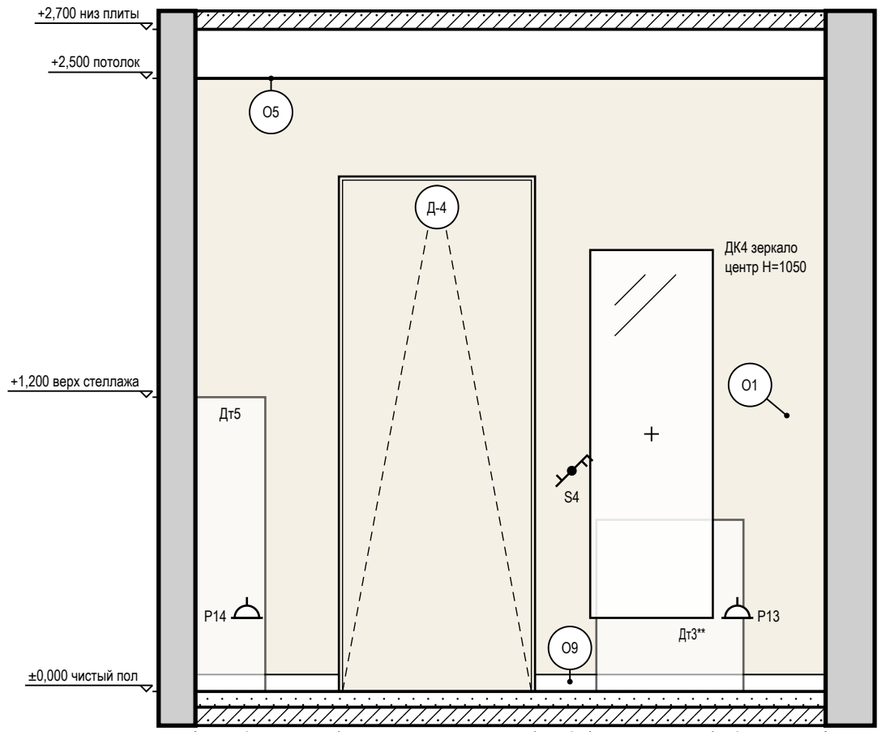

между чистовыми гранями: черновой 2600 − отделка 15 / 15

Стена Г (М 1:25)

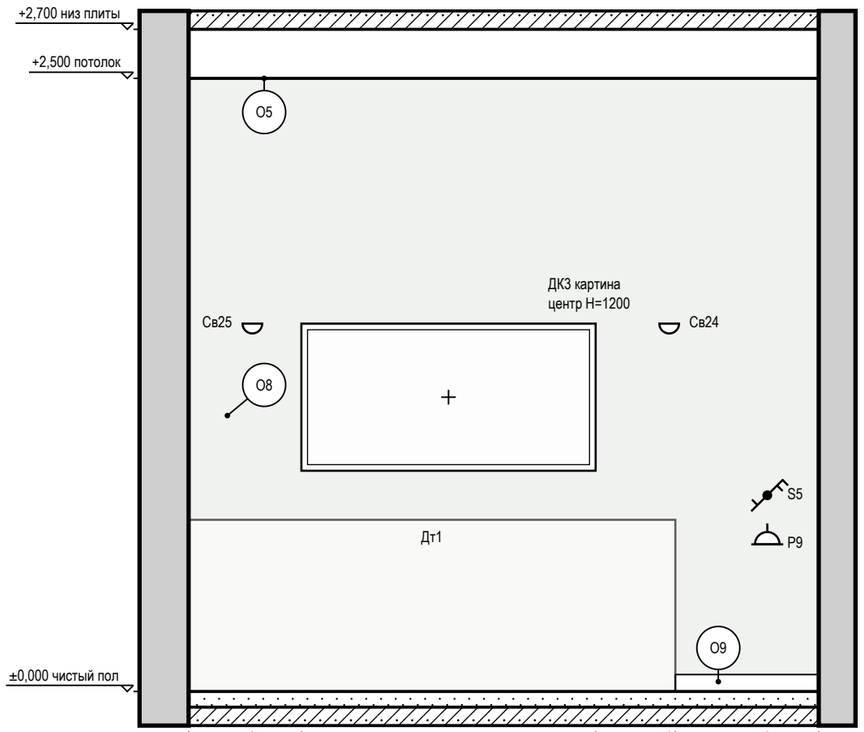


между чистовыми гранями: черновой 2600 − отделка 15 / 15

Условные обозначения

- розетка с заземляющим контактом; у знака марка, ×N — постов в рамке, гр. — группа щита, Н — высота оси, мм
- выключатель одноклавишный
- выключатель двухклавишный (флажков — по числу клавиш)
- выключатель с проходной или перекрёстной клавишей (обратный флажок); тип клавиши — в подписи
- светильник настенный (бра), Н — высота оси
- привязки точек и выводов от угла и от пола, мм
- мебель и приборы — фасад по расстановке (условно)
- картина (декор): марка Д, крест — центр, Н — высота центра, мм
- зеркало: марка Д, крест — центр, Н — высота центра, мм
- дверь скрытого монтажа: полотно в плоскости стены (узел — на листе узлов)
- стены и перекрытия в сечении
- окраска: тон — цвет по коду производителя (условно)
- О1 — марка отделки по реестру отделки альбома
- А — марка развёртки: буква стены, стрелка взгляд

Схема развёрток (М 1:50)

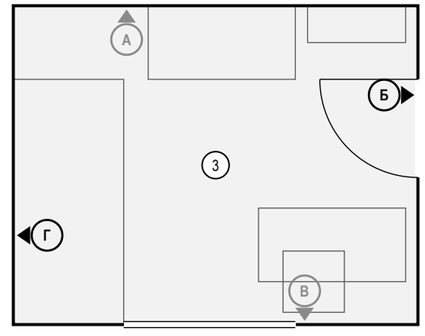

Ведомость точек и выводов

Стена	Марка	Что это	Гр.	Н, мм	От угла, мм	Примечание
Б	Р14	розетка: уборка у входа	5	300	210	
Б	S4	выключатель	1	900	1535	
Б	Р13	розетка: уборка	5	300	2210	
Г	Св25	светильник настенный	1	1500	260	

Стена	Марка	Что это	Гр.	Н, мм	От угла, мм	Примечание
Г	Св24	светильник настенный	1	1500	1960	
Г	Р9	розетка: у кровати	5	600	2360	
Г	S5	выключатель	1	800	2360	

Примечания

1. Развёртки — вид на стену изнутри помещения, по часовой стрелке; расположение — на схеме листа и на листе 83; размеры — в мм по чистовым поверхностям; отметки — в м от ±0,000; высоты Н — от чистого пола помещения до оси изделия, у декора — до центра.
2. Красная цепочка — привязки электроточек и выводов по осям от угла чистовых стен; высота Н — у знака, от чистого пола до оси; высоты мебели, проёмов и границ отделки — колонкой отметок слева. У знака — короткая марка; назначение, группа щита, высота и привязка каждой точки и вывода — в «Ведомости точек и выводов» под видами (каждая точка — строка).
3. Отделка стен — по ведомости отделки помещений, лист 61.
4. У знака электроточки: марка (Р — розетка, S — выключатель, Св — светильник, ЭВ — вывод кабеля), ×N — число постов в рамке, гр. — группа щита, Н — высота оси от чистого пола, мм; группы по клавишам выключателя — на листе выключателей.
5. Схема мебели, приборов и декора не является технической документацией для производства мебели; габариты — по паспортам изделий.
6. Картины и зеркала крепить к основанию по паспорту изделия (закладные и анкеры — в перечне скрытых работ); крест — ось центра предмета.
7. Двери скрытого монтажа — полотно в плоскости стены, отделка стены по полотну, плинтус прерывается у короба (узел — на листе узлов).
8. Потолок — у каждой стены свой, по плану потолков (ПТ1); ступени — зоной, кромка короба перед нишей — тонкой линией; в поле потолка: ПТ2 +2,600.

Допущения и предложения на листе. Знак «*» принято (замерить): окно пом. 3 (стена В). Знак «**» предложено (согласовать): дверь пом. 3 (стена Б). См. лист открытых вопросов (листы 6, 7).

1000 мм · печать 1:1

Изм.	Кол.уч	Лист	№ док.	Подп.	Дата
Разраб.		Кырлан А.С.			13.11.26
Пров.					
ГИП					
Н. контр.					
Утв.					

ГД-2026-011-АИ

Квартира 56 м²

ЖК «Северный парк», Москва

Дизайн-проект интерьера

Стадия	Лист	Листов
РП	93	119

Развёртки стен Б, Г. Детская (пом. 3)

М 1:25

Кырлан Александр Сергеевич


выпуск 13.11.2026 № eb78108814f · стр. 102 из 139

Развёртка стены В. Детская (пом. 3)

Детская (пом. 3) · вид изнутри помещения · размеры в мм, отметки в м

ПРЕДВАРИТЕЛЬНО · не для производства работ · открыто пунктов: 13 (реестр — л. 6, 7)

Стена В (М 1:20)

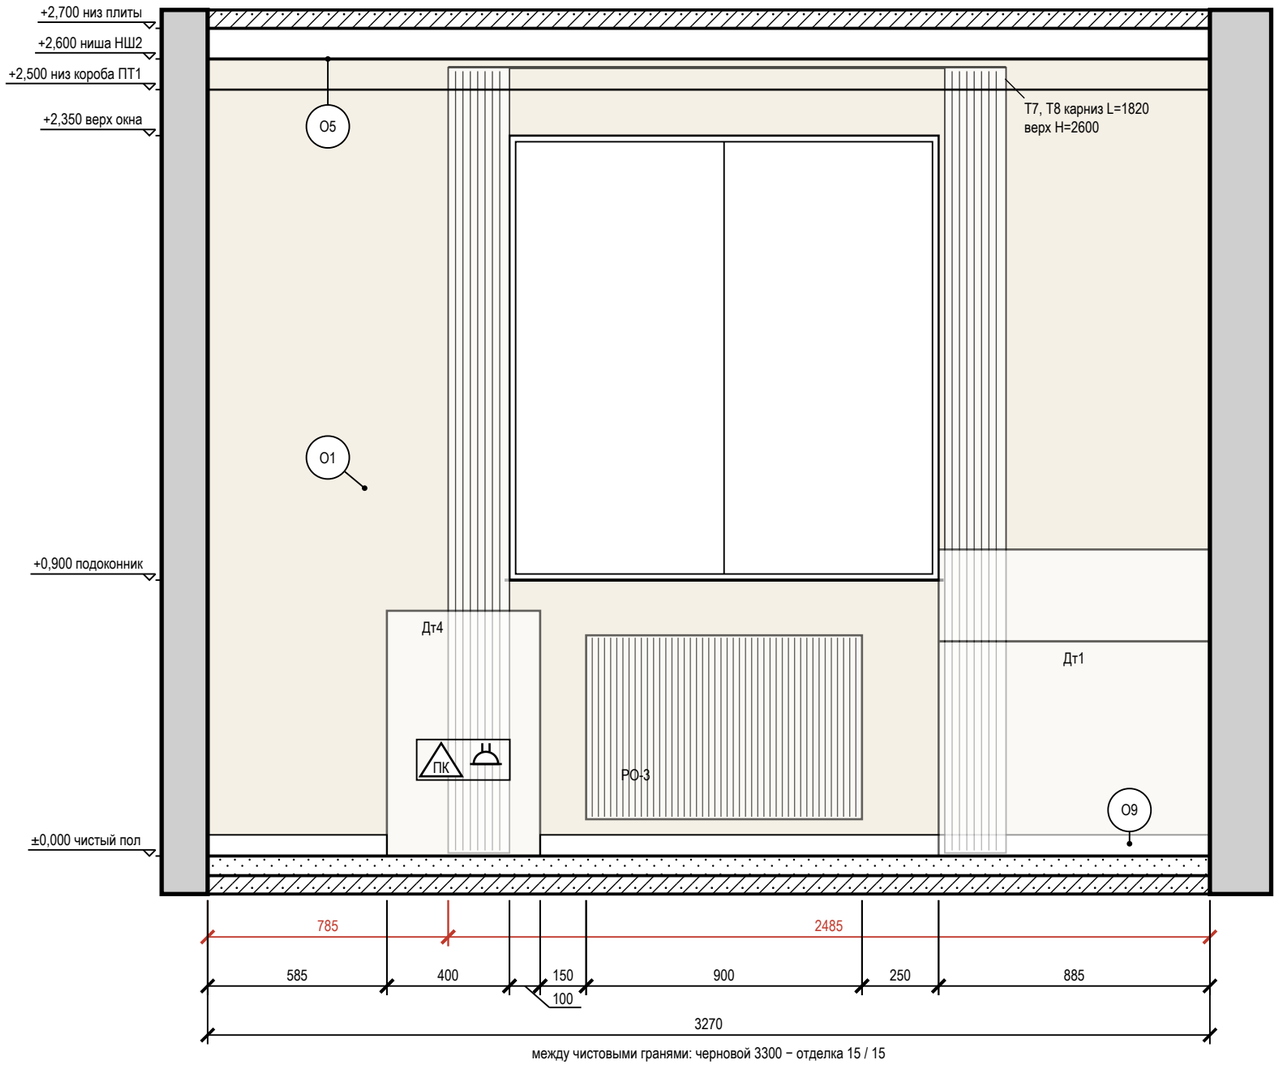

между чистовыми гранями: черновой 3300 − отделка 15 / 15

Ведомость точек и выводов

Марка	Что это	Гр.	H, мм	От угла, мм	Примечание
LAN2	розетка RJ45: рабочий стол		300	785	
P11	розетка: рабочий стол	5	300	885	рамка 2 поста


Условные обозначения

- розетка с заземляющим контактом; у знака марка, ×N — постов в рамке, гр. — группа щита, H — высота оси, мм
- ПК — розетка компьютерная RJ45
- привязки точек и выводов от угла и от пола, мм
- мебель и приборы — фасад по расстановке (условно)
- карниз (шина) и шторы в собранном виде: марка T, длина L, верх H
- окно: проём, рама, подоконник
- радиатор отопления; марка — по плану отопления
- стены и перекрытия в сечении
- окраска: тон — цвет по коду производителя (условно)
- О1 — марка отделки по реестру отделки альбома
- A — марка развёртки: буква стены, стрелка взгляд

Ведомость отделки (на листе)

Марка	Поверхность	Материал, изделие	Цвет, код	Кол.
О1	стены	окраска, Tikkurila Euro Power 7, колеровка по NCS, матовая, подготовка Q3	NCS S 0804-Y30R «S 0804-Y30R»	6,5 м²
О5	потолок	окраска, Tikkurila Euro Power 7, глубокоматовая, подготовка Q3	Tikkurila F485 «Damask»	8,6 м²
О9	плинтус	плинтус МДФ, Orac Decor Contour (Luxxus), h 69 мм, SX165	NCS S 0804-Y30R «S 0804-Y30R»	2,8 м

Схема развёрток (М 1:50)

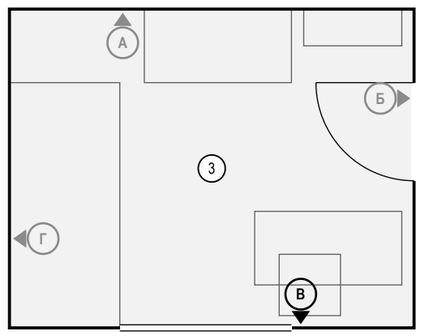

Примечания

1. Развёртки — вид на стену изнутри помещения, по часовой стрелке; расположение — на схеме листа и на листе 83; размеры — в мм по чистовым поверхностям; отметки — в м от ±0,000; высоты H — от чистого пола помещения до оси изделия, у декора — до центра.
2. Красная цепочка — привязки электроточек и выводов по осям от угла чистовых стен; высота H — у знака, от чистого пола до оси; высоты мебели, проёмов и границ отделки — колонкой отметок слева. У знака — короткая марка; назначение, группа щита, высота и привязка каждой точки и вывода — в «Ведомости точек и выводов» под видами (каждая точка — строка).
3. У знака электроточки: марка (Р — розетка, S — выключатель, Св — светильник, ЭВ — вывод кабеля), ×N — число постов в рамке, гр. — группа щита, H — высота оси от чистого пола, мм; группы по клавишам выключателя — на листе выключателей.
4. Схема мебели, приборов и декора не является технической документацией для производства мебели; габариты — по паспортам изделий.
5. Карнизы (шины) — по ведомости текстиля декоратора: длина L и верх H на развёртке — те же числа, что в ведомости; крепление — до окраски потолка.
6. Потолок — у каждой стены свой, по плану потолков (НШ2, ПТ1); ступени — зоной, кромка короба перед нишей — тонкой линией; в поле потолка: ПТ2 +2,600.
7. Линии узора (швы плитки, складки штор, рёбра радиаторов) прерываются у знаков и выносок — просвет между линиями не менее 0,7 мм.
8. Часть марок не уместилась у знаков: коды, высоты и привязки этих позиций — в ведомости точек и выводов под видами.

Допущения и предложения на листе. Основа листа: размеры помещений и положение проёмов введены заказчиком в брифе, на объекте не замерены (К-1); высота потолка 2700 мм — по брифу заказчика, не замерена (К-2); толщины стен приняты по брифу: наружные 200 мм, внутренние 150 мм — не обмерены (К-1); тип дома монолитный, перекрытие 200 мм — по брифу заказчика, документов нет (К-3); планировка (стены, проёмы, объединение кухни и гостиной, расширение санузла) — по брифу без обмера и плана БТИ (К-7); разрешённая мощность 10 кВт принята, ТУ не переданы (К-8); вентканалы приняты, в брифе не заданы (К-9); подрайон климата не задан — принят не северный (жилые от 2,5 м) (К-10). Знак «*» — принято, не замерено и не подтверждено (замерить на объекте): К-1: окно пом. 3 (стена В) — окно: положение, ширина, высота и подоконник — по брифу заказчика, не замерены. Знак «**» — предложение проектировщика, заказчиком не утверждено (согласовать с заказчиком): К-5: дверь пом. 3 (стена Б) — дверь в новой перегородке: проём по брифу, короб скрытой двери и размер в свету — после выбора модели и утверждения перегородки (К-5). См. лист открытых вопросов (лист 6, записи К-1–К-3, К-5, К-7–К-10).

1000 мм · печать 1:1

Изм.	Кол.уч	Лист	№ док.	Подп.	Дата
Разраб.		Кырлан А.С.			13.11.26
Пров.					
ГИП					
Н. контр.					
Утв.					

ГД-2026-011-АИ

Квартира 56 м²

ЖК «Северный парк», Москва

Дизайн-проект интерьера

Стадия	Лист	Листов
РП	94	119

Развёртка стены В. Детская (пом. 3)

М 1:20

Кырлан Александр Сергеевич


выпуск 13.11.2026 № eb78108814f · стр. 103 из 139

Развёртка стены А. Санузел (пом. 4)

Санузел (пом. 4) · вид изнутри помещения · размеры в мм, отметки в м

ПРЕДВАРИТЕЛЬНО · не для производства работ · открыто пунктов: 13 (реестр — л. 6, 7)

Стена А (М 1:20)

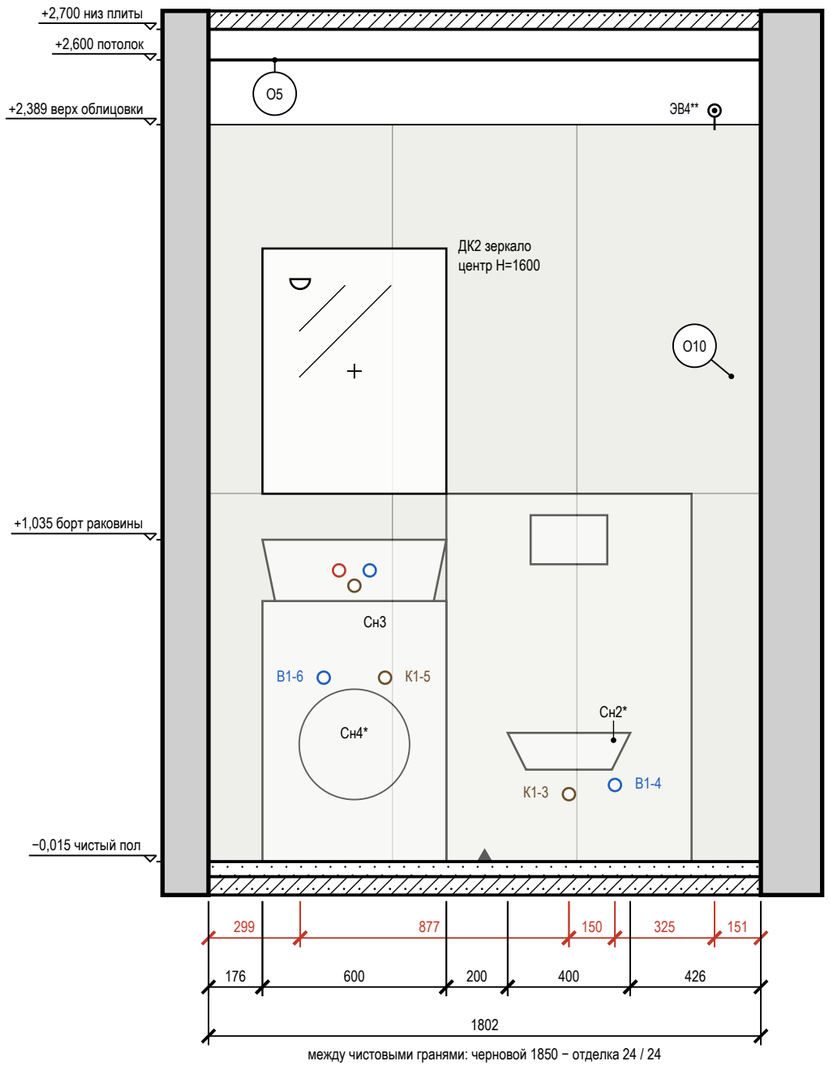

между чистовыми гранями: черновой 1850 − отделка 24 / 24

Ведомость точек и выводов

Марка	Что это	Гр.	Н, мм	От угла, мм	Примечание
Св15**	светильник настенный	3	1900	299	
В1-6	холодная вода — стиральная машина		600*	376	кран машины
Т3-3	горячая вода — умывальник		950*	426	межос. 100
К1-4	канализация — умывальник		900*	476	Ø50; плоский сифон, над машиной
В1-5	холодная вода — умывальник		950*	526	межос. 100
К1-5	канализация — стиральная машина		600*	576	Ø50
К1-3	канализация — унитаз подвесной		220*	1176	Ø110
В1-4	холодная вода — унитаз подвесной		250*	1326	в раме инсталляции
ЭВ4**	вывод кабеля: вентилятор ВР1 (таймер выбега)	3	2450	1651	


Условные обозначения

- вывод кабеля для подключения прибора (без розетки), марка ЭВ
- светильник настенный (бра), Н — высота оси
- вывод В1 (код — в ведомости привязок)
- вывод Т3 (код — в ведомости привязок)
- вывод К1 (код — в ведомости привязок)
- привязки точек и выводов от угла и от пола, мм
- мебель и приборы — фасад по расстановке (условно)
- зеркало: марка Д, крест — центр, Н — высота центра, мм
- стены и перекрытия в сечении
- плитка: сетка швов по формату, ▲ — ось старта
- О1 — марка отделки по реестру отделки альбома
- А — марка развёртки: буква стены, стрелка — взгляд

Ведомость отделки (на листе)

Марка	Поверхность	Материал, изделие	Цвет, код	Кол.
О5	потолок	окраска, Tikkurila Euro Power 7, матовая, подготовка Q3	Tikkurila F485 «Damask»	4,8 м²
О10	стены	облицовка плиткой, Atlas Concorde Marvel Travertine, 600×1200×9 мм, A8UZ, затирка CG2WA	Atlas Concorde A8UZ «Marvel Travertine»	4,3 м²

Схема развёрток (М 1:100)

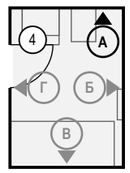

Примечания

1. Развёртки — вид на стену изнутри помещения, по часовой стрелке; расположение — на схеме листа и на листе 83; размеры — в мм по чистовым поверхностям; отметки — в м от ±0,000; высоты Н — от чистого пола помещения до оси изделия, у декора — до центра.
2. Красная цепочка — привязки электроточек и выводов по осям от угла чистовых стен; высота Н — у знака, от чистого пола до оси; высоты мебели, проёмов и границ отделки — колонкой отметок слева. У знака — короткая марка; назначение, группа щита, высота и привязка каждой точки и вывода — в «Ведомости точек и выводов» под видами (каждая точка — строка).
3. У знака электроточки: марка (Р — розетка, S — выключатель, Св — светильник, ЭВ — вывод кабеля), ×N — число постов в рамке, гр. — группа щита, Н — высота оси от чистого пола, мм; группы по клавишам выключателя — на листе выключателей.
4. Схема мебели, приборов и декора не является технической документацией для производства мебели; габариты — по паспортам изделий (* — высота не задана в проекте, показана по типовому изделию).
5. Выводы ВК — коды и высоты по листу выводов сантехники; * — высота принята по типовой практике монтажа, окончательно — по паспорту прибора.
6. Облицовка — по сетке швов 2 мм, раскладка от оси стены (треугольник у пола), целые ряды от пола; подрезки — по листу раскладки плитки.
7. Гидроизоляция в 2 слоя, заход на стены 200 мм; над ванной — до 2000 и 300 мм за борт — до облицовки, с актом скрытых работ и тестом проливом (узел — на листе узлов).
8. Картины и зеркала крепить к основанию по паспорту изделия (закладные и анкеры — в перечне скрытых работ); крест — ось центра предмета.
9. Часть марок не уместилась у знаков: коды, высоты и привязки этих позиций — в ведомости точек и выводов под видами.

Допущения и предложения на листе. Знак «**» предложено (согласовать): дверь пом. 4 (стена Г). См. лист открытых вопросов (листы 6, 7).

1000 мм · печать 1:1

Изм.	Кол.уч	Лист	№ док.	Подп.	Дата
Разраб.		Кырлан А.С.			13.11.26
Пров.					
ГИП					
Н. контр.					
Утв.					

ГД-2026-011-АИ

Квартира 56 м²

ЖК «Северный парк», Москва

Дизайн-проект интерьера

Стадия	Лист	Листов
РП	95	119

Развёртка стены А. Санузел (пом. 4)

М 1:20

Кырлан Александр Сергеевич


выпуск 13.11.2026 № eb7810814f · стр. 104 из 139

Развёртка стены Б. Санузел (пом. 4)

Санузел (пом. 4) · вид изнутри помещения · размеры в мм, отметки в м

ПРЕДВАРИТЕЛЬНО · не для производства работ · открыто пунктов: 13 (реестр — л. 6, 7)

Стена Б (М 1:20)

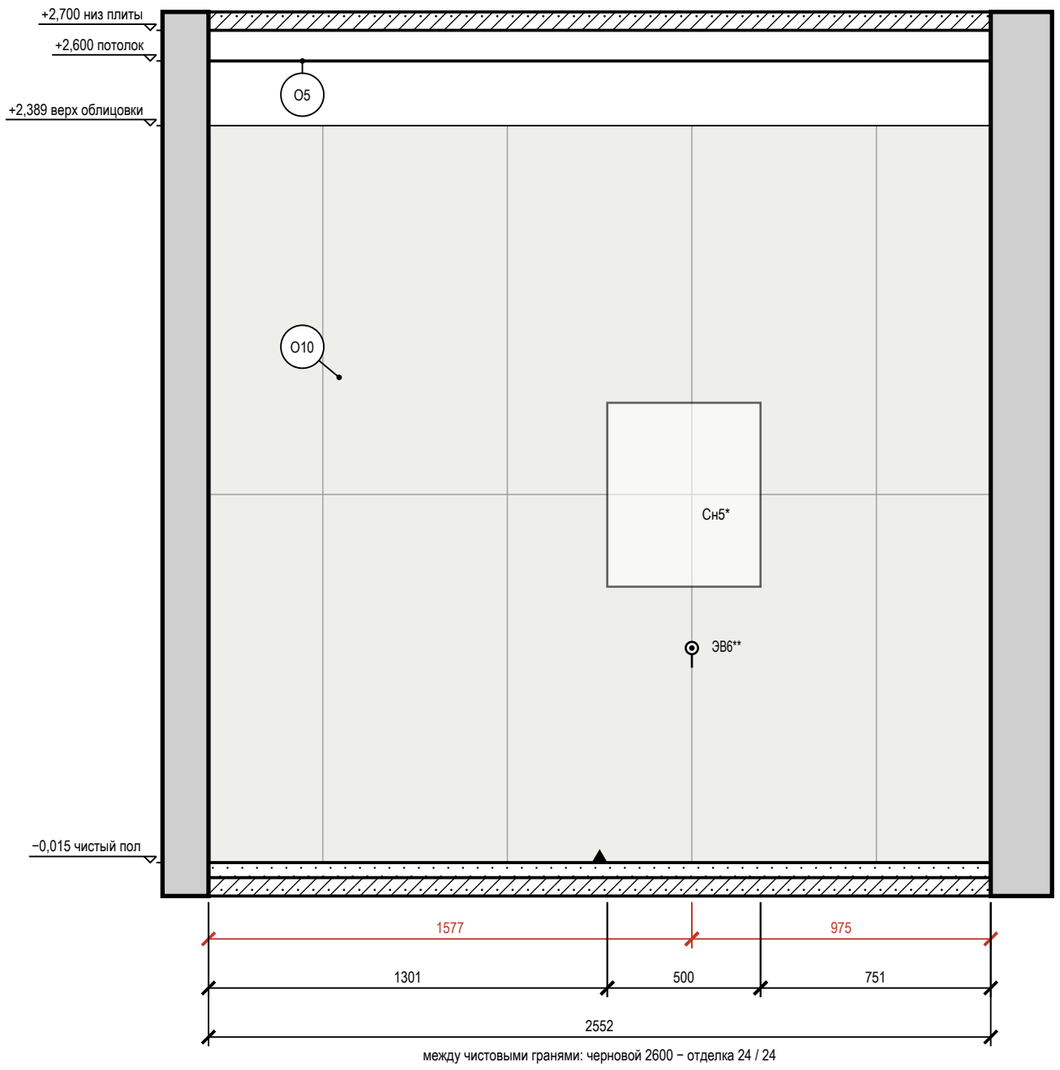

между чистовыми гранями: черновой 2600 − отделка 24 / 24

Ведомость точек и выводов

Марка	Что это	Гр.	Н, мм	От угла, мм	Примечание
ЭВ6**	вывод кабеля: полотенцесушитель Сн5	13	700	1577	


Условные обозначения

- вывод кабеля для подключения прибора (без розетки), марка ЭВ
- привязки точек и выводов от угла и от пола, мм
- мебель и приборы — фасад по расстановке (условно)
- стены и перекрытия в сечении
- плитка: сетка швов по формату, ▲ — ось старта
- О1 — марка отделки по реестру отделки альбома
- А — марка развёртки: буква стены, стрелка — взгляд

Ведомость отделки (на листе)

Марка	Поверхность	Материал, изделие	Цвет, код	Кол.
О5	потолок	окраска, Tikkurila Euro Power 7, матовая, подготовка Q3	Tikkurila F485 «Damask»	4,8 м²
О10	стены	облицовка плиткой, Atlas Concorde Marvel Travertine, 600×1200×9 мм, A8UZ, затирка CG2WA	Atlas Concorde A8UZ «Marvel Travertine»	6,1 м²

Схема развёрток (М 1:50)

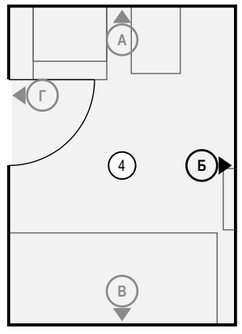

Допущения и предложения на листе

Основа листа: размеры помещений и положение проёмов введены заказчиком в брифе, на объекте не замерены (К-1); высота потолка 2700 мм — по брифу заказчика, не замерена (К-2); толщины стен приняты по брифу: наружные 200 мм, внутренние 150 мм — не обмерены (К-1); тип дома монолитный, перекрытие 200 мм — по брифу заказчика, документов нет (К-3); планировка (стены, проёмы, объединение кухни и гостиной, расширение санузла) — по брифу без обмера и плана БТИ (К-7); разрешённая мощность 10 кВт принята, ТУ не переданы (К-8); вентканалы приняты, в брифе не заданы (К-9); подрайон климата не задан — принят не северный (жилые от 2,5 м) (К-10).

Знак «**» — предложение проектировщика, заказчиком не утверждено (согласовать с заказчиком): ЭВ6 — по образцу: Добавлены электрические полотенцесушители IP44: П10 в ванной (480 мм, низ 900 мм) и П13 в санузле 2 (400 мм, низ 900 мм), выводы ЭВ6 и ЭВ7; мощность группы 13 — 2,4 кВт вместо 1,8 кВт; сдвиг под раскладку плитки стены Б на 126 мм вдоль стены — ось на шве или в центре плитки, привязка по таблице листа; К-5: дверь пом. 4 (стена Г) — дверь в новой перегородке: проём по брифу, короб скрытой двери и размер в свету — после выбора модели и утверждения перегородки (К-5).

См. лист открытых вопросов (лист 6, записи К-1–К-3, К-5, К-7–К-10).

Ведомость изделий и проёмов (на листе)

Марка	Изделие, проём	На виде Ш×В, мм	Низ, мм
Сн5*	полотенцесушитель электрический 500×1050, чёрный	500×600	900

Примечания

1. Развёртки — вид на стену изнутри помещения, по часовой стрелке; расположение — на схеме листа и на листе 83; размеры — в мм по чистовым поверхностям; отметки — в м от ±0,000; высоты Н — от чистого пола помещения до оси изделия, у декора — до центра.
2. Красная цепочка — привязки электроточек и выводов по осям от угла чистовых стен; высота Н — у знака, от чистого пола до оси; высоты мебели, проёмов и границ отделки — колонкой отметок слева. У знака — короткая марка; назначение, группа щита, высота и привязка каждой точки и вывода — в «Ведомости точек и выводов» под видами (каждая точка — строка).
3. У знака электроточки: марка (Р — розетка, S — выключатель, Св — светильник, ЭВ — вывод кабеля), ×N — число постов в рамке, гр. — группа щита, Н — высота оси от чистого пола, мм; группы по клавишам выключателя — на листе выключателей.
4. Схема мебели, приборов и декора не является технической документацией для производства мебели; габариты — по паспортам изделий (* — высота не задана в проекте, показана по типовому изделию).
5. Облицовка — по сетке швов 2 мм, раскладка от оси стены (треугольник у пола), целые ряды от пола; подрезки — по листу раскладки плитки.
6. Гидроизоляция в 2 слоя, заход на стены 200 мм; над ванной — до 2000 и 300 мм за борт — до облицовки, с актом скрытых работ и тестом проливом (узел — на листе узлов).

1000 мм · печать 1:1

Изм.	Кол.уч	Лист	№ док.	Подп.	Дата
Разраб.		Кырлан А.С.			13.11.26
Пров.					
ГИП					
Н. контр.					
Утв.					

ГД-2026-011-АИ

Квартира 56 м²

ЖК «Северный парк», Москва

Дизайн-проект интерьера

Стадия	Лист	Листов
РП	96	119

Развёртка стены Б. Санузел (пом. 4)

М 1:20

Кырлан Александр Сергеевич


выпуск 13.11.2026 № eb7810814f · стр. 105 из 139

Развёртки стен В, Г. Санузел (пом. 4)

Санузел (пом. 4) · вид изнутри помещения · размеры в мм, отметки в м


ПРЕДВАРИТЕЛЬНО · не для производства работ · открыто пунктов: 13 (реестр — л. 6, 7)

Стена В (М 1:25)

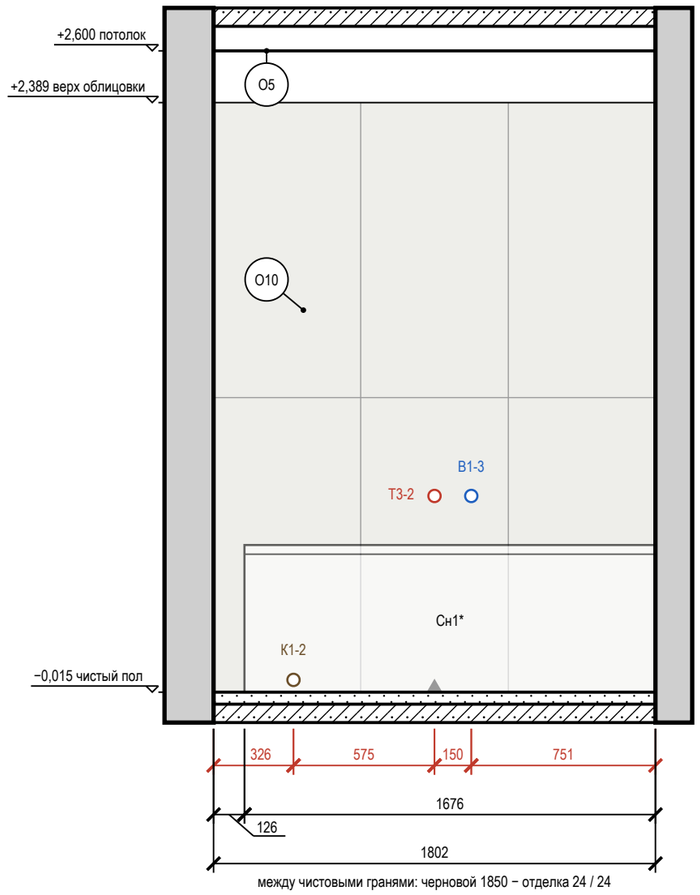

между чистовыми гранями: черновой 1850 − отделка 24 / 24

Стена Г (М 1:25)

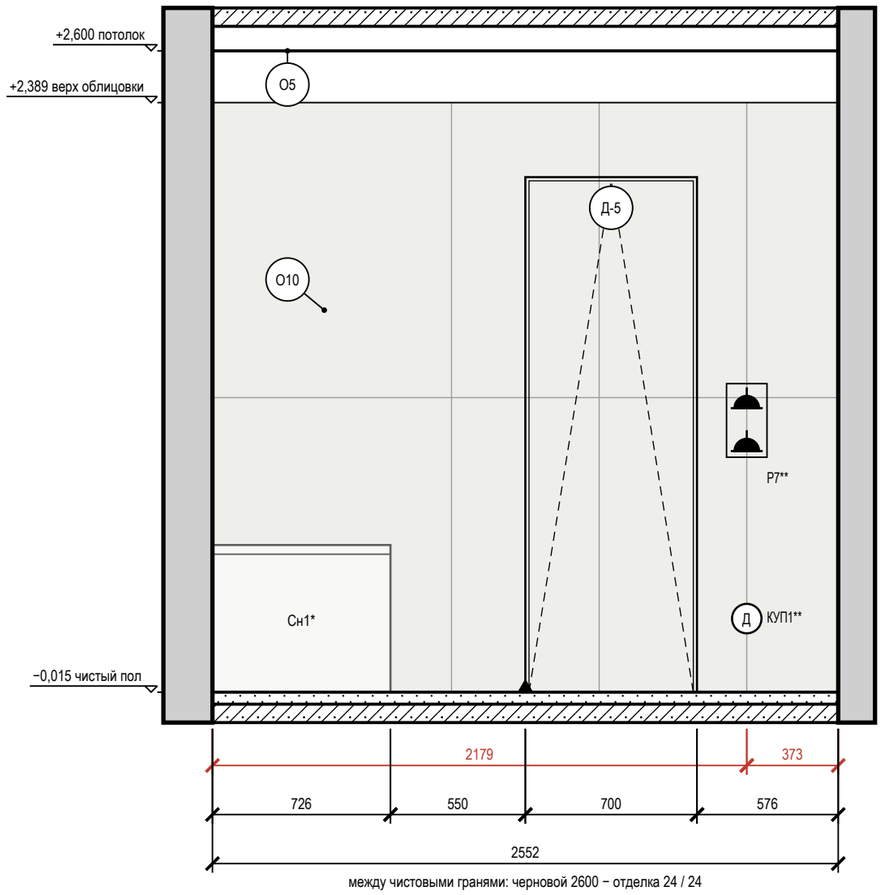


между чистовыми гранями: черновой 2600 − отделка 24 / 24

Условные обозначения

- розетка влагозащищённая IP44
- вывод В1 (код — в ведомости привязок)
- вывод Т3 (код — в ведомости привязок)
- вывод К1 (код — в ведомости привязок)
- привязки точек и выводов от угла и от пола, мм
- мебель и приборы — фасад по расстановке (условно)
- дверь скрытого монтажа: полотно в плоскости стены (узел — на листе узлов)
- стены и перекрытия в сечении
- плитка: сетка швов по формату, ▲ — ось старта
- О1 — марка отделки по реестру отделки альбома
- А — марка развёртки: буква стены, стрелка — взгляд

Схема развёрток (М 1:50)

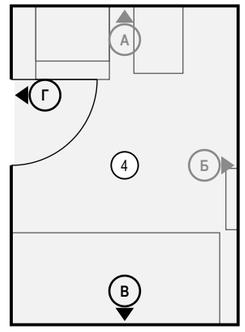

Ведомость точек и выводов

Стена	Марка	Что это	Гр.	Н, мм	От угла, мм	Примечание
В	К1-2	канализация — ванна		50*	326	Ø50
В	Т3-2	горячая вода — ванна		800*	901	межос. 150
В	В1-3	холодная вода — ванна		800*	1051	межос. 150
Г	КУП1**	КУП (уравнивание потенциалов): КУП уравнивание потенциалов (ДСУП)		300	2179	
Г	Р7**	розетка: стиральная машина	12	1000	2179	IP44
Г	Р8**	розетка: фен у умывальника	13	1141	2179	IP44

Ведомость изделий и проёмов (на листе)

Стена	Марка	Изделие, проём	На виде Ш×В, мм	Низ, мм
В	Сн1*	ванна 1700×750 акриловая, экран под плитку	1676×600	0
Г	Сн1*	ванна 1700×750 акриловая, экран под плитку	726×600	0
Г	Д-5	дверь скрытого монтажа	700×2100	0

Примечания

1. Развёртки — вид на стену изнутри помещения, по часовой стрелке; расположение — на схеме листа и на листе 83; размеры — в мм по чистовым поверхностям; отметки — в м от ±0,000; высоты Н — от чистого пола помещения до оси изделия, у декора — до центра.
2. Красная цепочка — привязки электроточек и выводов по осям от угла чистовых стен; высота Н — у знака, от чистого пола до оси; высоты мебели, проёмов и границ отделки — колонкой отметок слева. У знака — короткая марка; назначение, группа щита, высота и привязка каждой точки и вывода — в «Ведомости точек и выводов» под видами (каждая точка — строка).
3. Отделка стен — по ведомости отделки помещений, лист 61.
4. У знака электроточки: марка (Р — розетка, S — выключатель, Св — светильник, ЭВ — вывод кабеля), ×N — число постов в рамке, гр. — группа щита, Н — высота оси от чистого пола, мм; группы по клавишам выключателя — на листе выключателей.
5. Схема мебели, приборов и декора не является технической документацией для производства мебели; габариты — по паспортам изделий (* — высота не задана в проекте, показана по типовому изделию).
6. Выводы ВК — коды и высоты по листу выводов сантехники; * — высота принята по типовой практике монтажа, окончательно — по паспорту прибора.
7. Облицовка — по сетке швов 2 мм, раскладка от оси стены (треугольник у пола), целые ряды от пола; подрезки — по листу раскладки плитки.
8. Гидроизоляция в 2 слоя, заход на стены 200 мм; над ванной — до 2000 и 300 мм за борт — до облицовки, с актом скрытых работ и тестом проливом (узел — на листе узлов).
9. Двери скрытого монтажа — полотно в плоскости стены, отделка стены по полотну, плинтус прерывается у короба (узел — на листе узлов).
10. Часть марок не уместилась у знаков: коды, высоты и привязки этих позиций — в ведомости точек и выводов под видами.

Допущения и предложения на листе. Знак «**» предложено (согласовать): дверь пом. 4 (стена Г). См. лист открытых вопросов (листы 6, 7).

1000 мм · печать 1:1

Изм.	Кол.уч	Лист	№ док.	Подп.	Дата
Разраб.		Кырлан А.С.			13.11.26
Пров.					
ГИП					
Н. контр.					
Утв.					

ГД-2026-011-АИ

Квартира 56 м²

ЖК «Северный парк», Москва

Дизайн-проект интерьера

Стадия	Лист	Листов
РП	97	119

Развёртки стен В, Г. Санузел (пом. 4)

М 1:25

Кырлан Александр Сергеевич


выпуск 13.11.2026 № eb78108814f · стр. 106 из 139

Развёртка стены А. Прихожая (пом. 5)

Прихожая (пом. 5) · вид изнутри помещения · размеры в мм, отметки в м

ПРЕДВАРИТЕЛЬНО · не для производства работ · открыто пунктов: 13 (реестр — л. 6, 7)

Стена А (М 1:20)

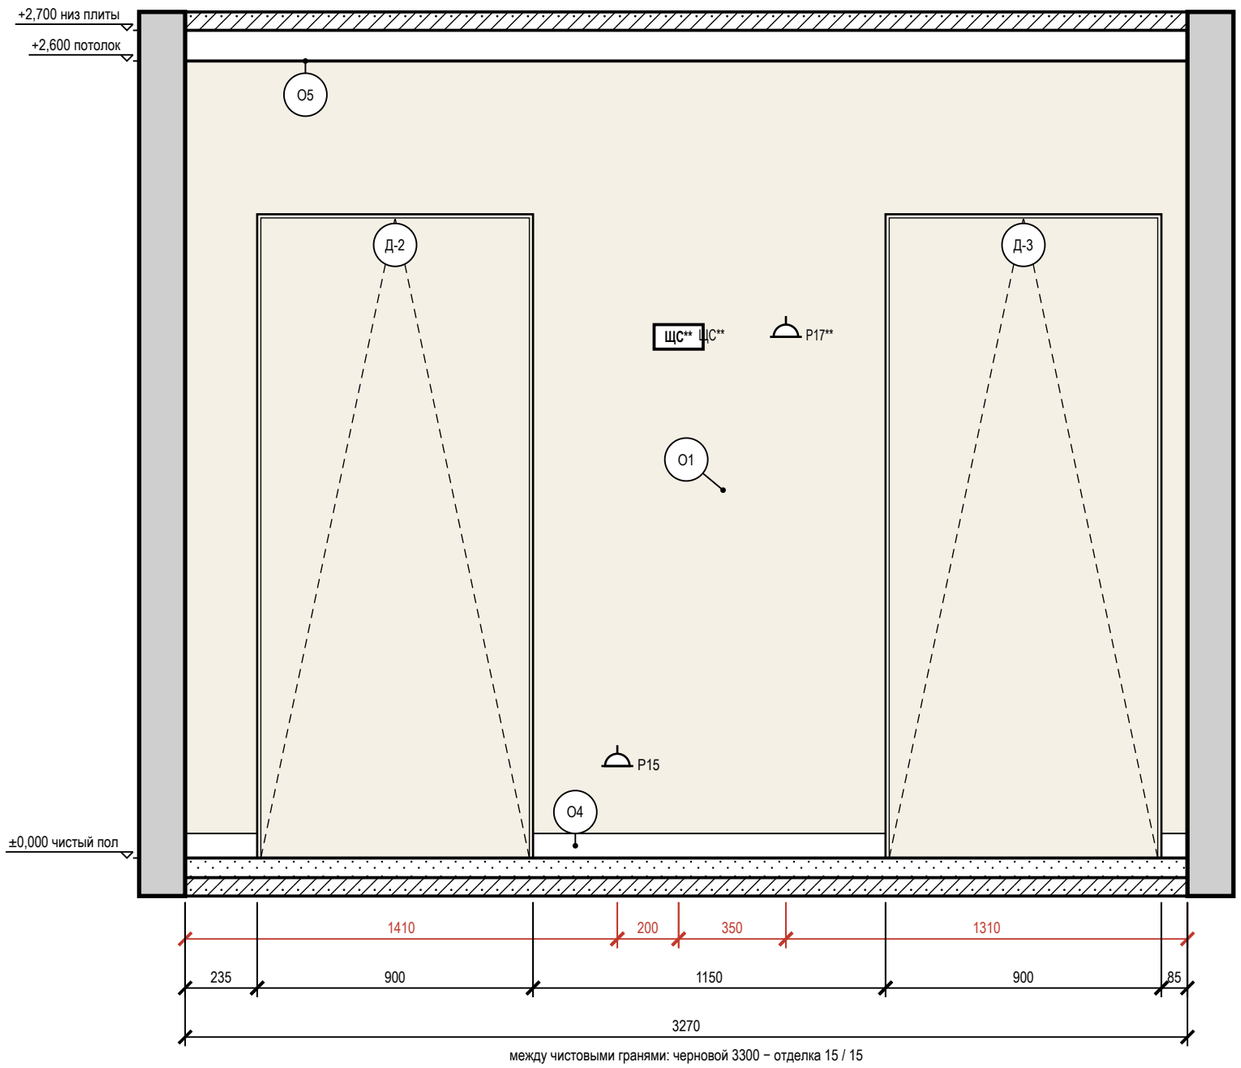

между чистовыми гранями: черновой 3300 − отделка 15 / 15

Ведомость точек и выводов

Марка	Что это	Гр.	Н, мм	От угла, мм	Примечание
Р15	розетка: пылесос, сушилка обуви	6	300	1410	
ЩС**	щит: щит слаботочный: ввод оптики, ONT, роутер, патч-панель		1700	1610	
Р17**	розетка: питание слаботочного щита (рядом с ЩС**)	14	1700	1960	


Условные обозначения

- розетка с заземляющим контактом; у знака — марка, ×N постов в рамке, гр. — группа щита, Н — высота оси, мм
- ЩК — щит квартирный
- привязки точек и выводов от угла и от пола, мм
- мебель и приборы — фасад по расстановке (условно)
- дверь скрытого монтажа: полотно в плоскости стены (узел — на листе узлов)
- стены и перекрытия в сечении
- окраска: тон — цвет по коду производителя (условно)
- О1 — марка отделки по реестру отделки альбома
- А — марка развёртки: буква стены, стрелка — взгляд

Ведомость отделки (на листе)

Марка	Поверхность	Материал, изделие	Цвет, код	Кол.
О1	стены	окраска, Tikkurila Euro Power 7, колеровка по NCS, матовая, подготовка Q3	NCS S 0804-Y30R «S 0804-Y30R»	4,7 м²
О4	плинтус	плинтус МДФ, h 80 мм, аналог: плинтус МДФ под покраску 80×16	NCS S 0804-Y30R «S 0804-Y30R»	1,5 м
О5	потолок	окраска, Tikkurila Euro Power 7, глубокоматовая, подготовка Q3	Tikkurila F485 «Damask»	8,6 м²

Схема развёрток (М 1:50)

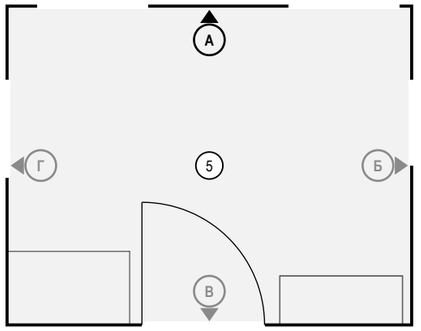

Примечания

1. Развёртки — вид на стену изнутри помещения, по часовой стрелке; расположение — на схеме листа и на листе 83; размеры — в мм по чистовым поверхностям; отметки — в м от ±0,000; высоты Н — от чистого пола помещения до оси изделия, у декора — до центра.
2. Красная цепочка — привязки электроточек и выводов по осям от угла чистовых стен; высота Н — у знака, от чистого пола до оси; высоты мебели, проёмов и границ отделки — колонкой отметок слева. У знака — короткая марка; назначение, группа щита, высота и привязка каждой точки и вывода — в «Ведомости точек и выводов» под видами (каждая точка — строка).
3. У знака электроточки: марка (Р — розетка, S — выключатель, Св — светильник, ЭВ — вывод кабеля), ×N — число постов в рамке, гр. — группа щита, Н — высота оси от чистого пола, мм; группы по клавишам выключателя — на листе выключателей.
4. Схема мебели, приборов и декора не является технической документацией для производства мебели; габариты — по паспортам изделий.
5. Двери скрытого монтажа — полотно в плоскости стены, отделка стены по полотну, плинтус прерывается у короба (узел — на листе узлов).

Допущения и предложения на листе

Основа листа: размеры помещений и положение проёмов введены заказчиком в брифе, на объекте не замерены (К-1); высота потолка 2700 мм — по брифу заказчика, не замерена (К-2); толщины стен приняты по брифу: наружные 200 мм, внутренние 150 мм — не обмерены (К-1); тип дома монолитный, перекрытие 200 мм — по брифу заказчика, документов нет (К-3); планировка (стены, проёмы, объединение кухни и гостиной, расширение санузла) — по брифу без обмера и плана БТИ (К-7); разрешённая мощность 10 кВт принята, ТУ не переданы (К-8); вентканалы приняты, в брифе не заданы (К-9); подрайон климата не задан — принят не северный (жилые от 2,5 м) (К-10).

Знак «*» — принято, не замерено и не подтверждено (замерить на объекте): К-1: дверь пом. 5 (стена В) — входная дверь: положение и ширина проёма — по брифу заказчика, не замерены.

Знак «**» — предложение проектировщика, заказчиком не утверждено (согласовать с заказчиком): Р17 — высота 1700 мм выше нормы 1 м (ПУЭ 6.6.30) по назначению: питание слаботочного щита ЩС, рядом со щитом на его высоте; ЩС — щит слаботочный: место и состав.

См. лист открытых вопросов (лист 6, записи К-1–К-3, К-7–К-10).

1000 мм · печать 1:1

Изм.	Кол.уч	Лист	№ док.	Подп.	Дата
Разраб.		Кырлан А.С.			13.11.26
Пров.					
ГИП					
Н. контр.					
Утв.					

ГД-2026-011-АИ

Квартира 56 м²

ЖК «Северный парк», Москва

Дизайн-проект интерьера

Стадия	Лист	Листов
РП	98	119

Развёртка стены А. Прихожая (пом. 5)

М 1:20

Кырлан Александр Сергеевич


выпуск 13.11.2026 № eb7810814f · стр. 107 из 139

Развёртка стены Б. Прихожая (пом. 5)

Прихожая (пом. 5) · вид изнутри помещения · размеры в мм, отметки в м

ПРЕДВАРИТЕЛЬНО · не для производства работ · открыто пунктов: 13 (реестр — л. 6, 7)

Стена Б (М 1:20)

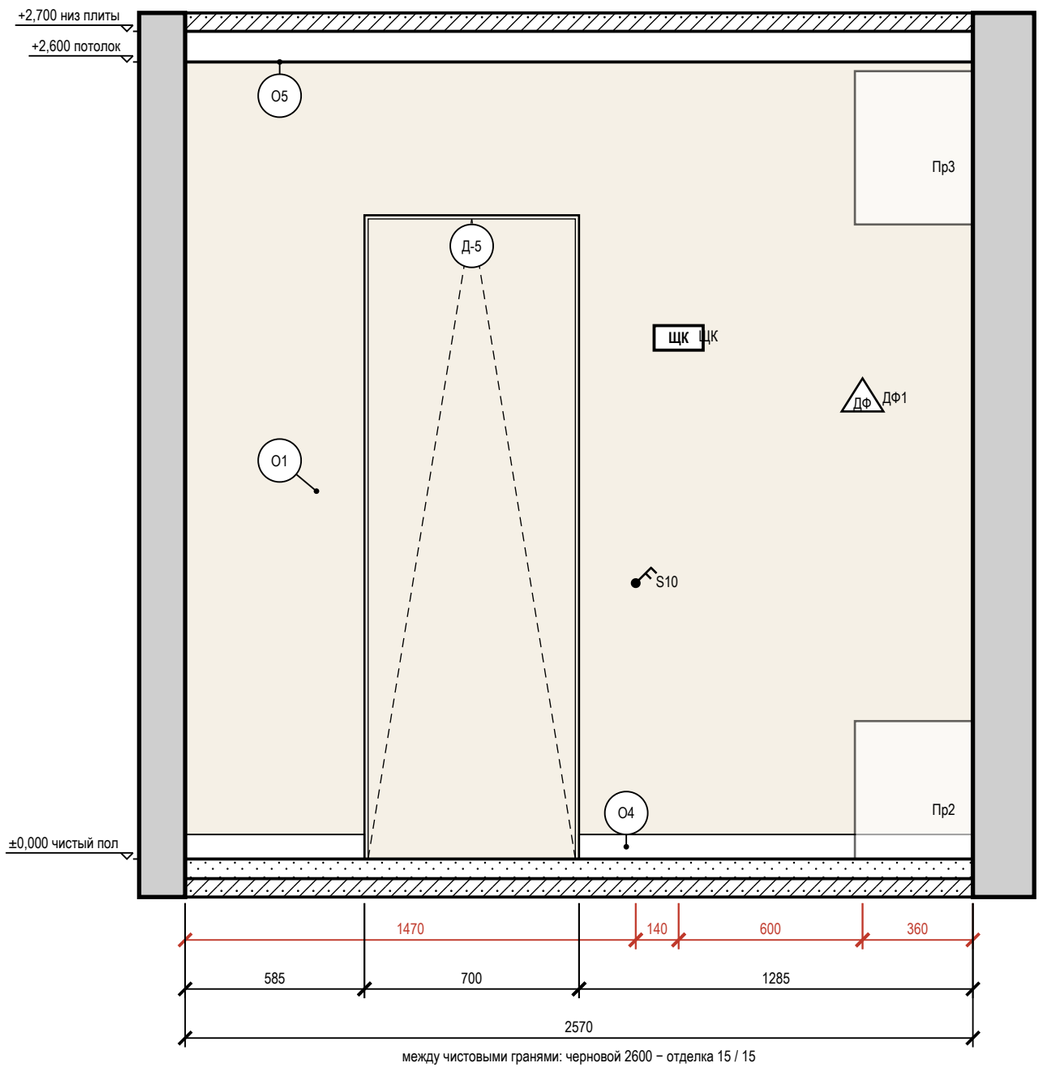

между чистовыми гранями: черновой 2600 − отделка 15 / 15

Ведомость точек и выводов

Марка	Что это	Гр.	Н, мм	От угла, мм	Примечание
S10	выключатель	3	900	1470	
ЩК	щит: щит квартирный ЩРВ-П-48		1700	1610	
ДФ1	домофон: трубка домофона		1500	2210	


Условные обозначения

- выключатель одноклавишный
- выключатель двухклавишный (флажков — по числу клавиш)
- ДФ — трубка или монитор домофона
- ЩК — щит квартирный
- привязки точек и выводов от угла и от пола, мм
- мебель и приборы — фасад по расстановке (условно)
- дверь скрытого монтажа: полотно в плоскости стены (узел — на листе узлов)
- стены и перекрытия в сечении
- окраска: тон — цвет по коду производителя (условно)
- О1 — марка отделки по реестру отделки альбома
- А — марка развёртки: буква стены, стрелка — взгляд

Ведомость отделки (на листе)

Марка	Поверхность	Материал, изделие	Цвет, код	Кол.
О1	стены	окраска, Tikkurila Euro Power 7, колеровка по NCS, матовая, подготовка Q3	NCS S 0804-Y30R «S 0804-Y30R»	5,2 м²
О4	плинтус	плинтус МДФ, h 80 мм, аналог: плинтус МДФ под покраску 80×16	NCS S 0804-Y30R «S 0804-Y30R»	1,9 м
О5	потолок	окраска, Tikkurila Euro Power 7, глубокоматовая, подготовка Q3	Tikkurila F485 «Damask»	8,6 м²

Схема развёрток (М 1:50)

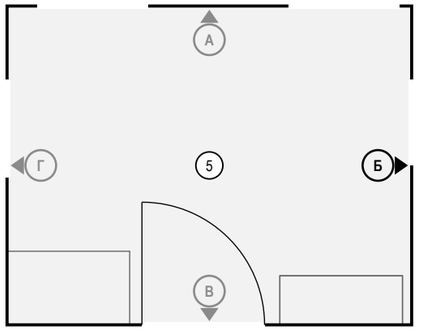

Примечания

1. Развёртки — вид на стену изнутри помещения, по часовой стрелке; расположение — на схеме листа и на листе 83; размеры — в мм по чистовым поверхностям; отметки — в м от ±0,000; высоты Н — от чистого пола помещения до оси изделия, у декора — до центра.
2. Красная цепочка — привязки электроточек и выводов по осям от угла чистовых стен; высота Н — у знака, от чистого пола до оси; высоты мебели, проёмов и границ отделки — колонкой отметок слева. У знака — короткая марка; назначение, группа щита, высота и привязка каждой точки и вывода — в «Ведомости точек и выводов» под видами (каждая точка — строка).
3. У знака электроточки: марка (Р — розетка, S — выключатель, Св — светильник, ЭВ — вывод кабеля), ×N — число постов в рамке, гр. — группа щита, Н — высота оси от чистого пола, мм; группы по клавишам выключателя — на листе выключателей.
4. Схема мебели, приборов и декора не является технической документацией для производства мебели; габариты — по паспортам изделий.
5. Двери скрытого монтажа — полотно в плоскости стены, отделка стены по полотну, плинтус прерывается у короба (узел — на листе узлов).

Допущения и предложения на листе

Основа листа: размеры помещений и положение проёмов введены заказчиком в брифе, на объекте не замерены (К-1); высота потолка 2700 мм — по брифу заказчика, не замерена (К-2); толщины стен приняты по брифу: наружные 200 мм, внутренние 150 мм — не обмерены (К-1); тип дома монолитный, перекрытие 200 мм — по брифу заказчика, документов нет (К-3); планировка (стены, проёмы, объединение кухни и гостиной, расширение санузла) — по брифу без обмера и плана БТИ (К-7); разрешённая мощность 10 кВт принята, ТУ не переданы (К-8); вентканалы приняты, в брифе не заданы (К-9); подрайон климата не задан — принят не северный (жилые от 2,5 м) (К-10).

Знак «*» — принято, не замерено и не подтверждено (замерить на объекте): К-1: дверь пом. 5 (стена В) — входная дверь: положение и ширина проёма — по брифу заказчика, не замерены.

См. лист открытых вопросов (лист 6, записи К-1–К-3, К-7–К-10).

1000 мм · печать 1:1

Изм.	Кол.уч	Лист	№ док.	Подп.	Дата
Разраб.		Кырлан А.С.			13.11.26
Пров.					
ГИП					
Н. контр.					
Утв.					

ГД-2026-011-АИ

Квартира 56 м²

ЖК «Северный парк», Москва

Дизайн-проект интерьера

Стадия	Лист	Листов
РП	99	119

Развёртка стены Б. Прихожая (пом. 5)

М 1:20

Кырлан Александр Сергеевич


выпуск 13.11.2026 № eb7810814f · стр. 108 из 139

Развёртка стены В. Прихожая (пом. 5)

Прихожая (пом. 5) · вид изнутри помещения · размеры в мм, отметки в м

ПРЕДВАРИТЕЛЬНО · не для производства работ · открыто пунктов: 13 (реестр — л. 6, 7)

Стена В (М 1:20)

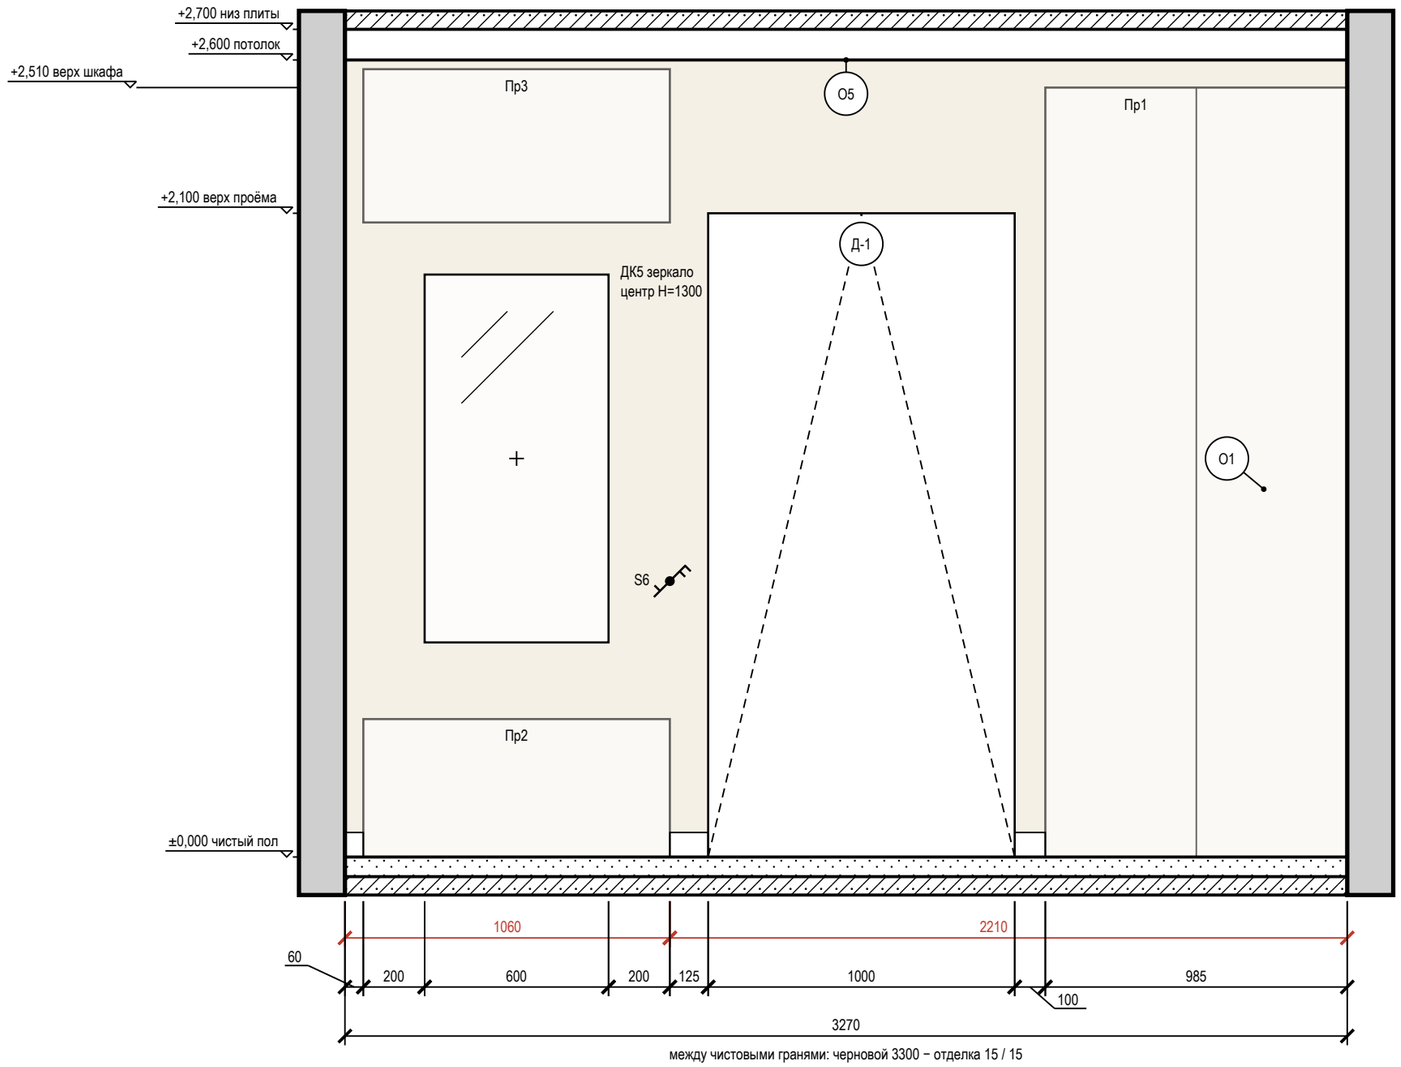

между чистовыми гранями: черновой 3300 − отделка 15 / 15

Ведомость точек и выводов

Марка	Что это	Гр.	Н, мм	От угла, мм	Примечание
S6	выключатель	2	900	1060	


Условные обозначения

- выключатель одноклавишный
- выключатель двухклавишный (флажков — по числу клавиш)
- выключатель с проходной или перекрёстной клавишей (обратный флажок); тип клавиши — в подписи
- привязки точек и выводов от угла и от пола, мм
- мебель и приборы — фасад по расстановке (условно)
- зеркало: марка Д, крест — центр, Н — высота центра, мм
- дверной проём; марка двери — в кружке
- стены и перекрытия в сечении
- окраска: тон — цвет по коду производителя (условно)
- О1 — марка отделки по реестру отделки альбома
- А — марка развёртки: буква стены, стрелка взгляд

Ведомость отделки (на листе)

Марка	Поверхность	Материал, изделие	Цвет, код	Кол.
О1	стены	окраска, Tikkurila Euro Power 7, колеровка по NCS, матовая, подготовка Q3	NCS S 0804-Y30R «S 0804-Y30R»	3,8 м²
О4	плинтус	плинтус МДФ, h 80 мм, аналог: плинтус МДФ под покраску 80×16	NCS S 0804-Y30R «S 0804-Y30R»	0,3 м
О5	потолок	окраска, Tikkurila Euro Power 7, глубокоматовая, подготовка Q3	Tikkurila F485 «Damask»	8,6 м²

Схема развёрток (М 1:100)

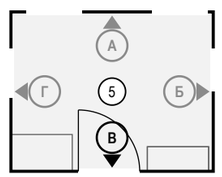

Примечания

1. Развёртки — вид на стену изнутри помещения, по часовой стрелке; расположение — на схеме листа и на листе 83; размеры — в мм по чистовым поверхностям; отметки — в м от ±0,000; высоты Н — от чистого пола помещения до оси изделия, у декора — до центра.
2. Красная цепочка — привязки электроточек и выводов по осям от угла чистовых стен; высота Н — у знака, от чистого пола до оси; высоты мебели, проёмов и границ отделки — колонкой отметок слева. У знака — короткая марка; назначение, группа щита, высота и привязка каждой точки и вывода — в «Ведомости точек и выводов» под видами (каждая точка — строка).
3. У знака электроточки: марка (Р — розетка, S — выключатель, Св — светильник, ЭВ — вывод кабеля), ×N — число постов в рамке, гр. — группа щита, Н — высота оси от чистого пола, мм; группы по клавишам выключателя — на листе выключателей.
4. Схема мебели, приборов и декора не является технической документацией для производства мебели; габариты — по паспортам изделий.
5. Картины и зеркала крепить к основанию по паспорту изделия (закладные и анкеры — в перечне скрытых работ); крест — ось центра предмета.

Допущения и предложения на листе

Основа листа: размеры помещений и положение проёмов введены заказчиком в брифе, на объекте не замерены (К-1); высота потолка 2700 мм — по брифу заказчика, не замерена (К-2); толщины стен приняты по брифу: наружные 200 мм, внутренние 150 мм — не обмерены (К-1); тип дома монолитный, перекрытие 200 мм — по брифу заказчика, документов нет (К-3); планировка (стены, проёмы, объединение кухни и гостиной, расширение санузла) — по брифу без обмера и плана БТИ (К-7); разрешённая мощность 10 кВт принята, ТУ не переданы (К-8); вентканалы приняты, в брифе не заданы (К-9); подрайон климата не задан — принят не северный (жилые от 2,5 м) (К-10).

Знак «*» — принято, не замерено и не подтверждено (замерить на объекте): К-1: дверь пом. 5 (стена В) — входная дверь: положение и ширина проёма — по брифу заказчика, не замерены.

См. лист открытых вопросов (лист 6, записи К-1–К-3, К-7–К-10).

1000 мм · печать 1:1

Изм.	Кол.уч	Лист	№ док.	Подп.	Дата
Разраб.		Кырлан А.С.			13.11.26
Пров.					
ГИП					
Н. контр.					
Утв.					

ГД-2026-011-АИ

Квартира 56 м²

ЖК «Северный парк», Москва

Дизайн-проект интерьера

Стадия	Лист	Листов
РП	100	119

Развёртка стены В. Прихожая (пом. 5)

М 1:20

Кырлан Александр Сергеевич


выпуск 13.11.2026 № eb7810814f · стр. 109 из 139

Развёртка стены Г. Прихожая (пом. 5)

Прихожая (пом. 5) · вид изнутри помещения · размеры в мм, отметки в м

ПРЕДВАРИТЕЛЬНО · не для производства работ · открыто пунктов: 13 (реестр — л. 6, 7)

Стена Г (М 1:20)

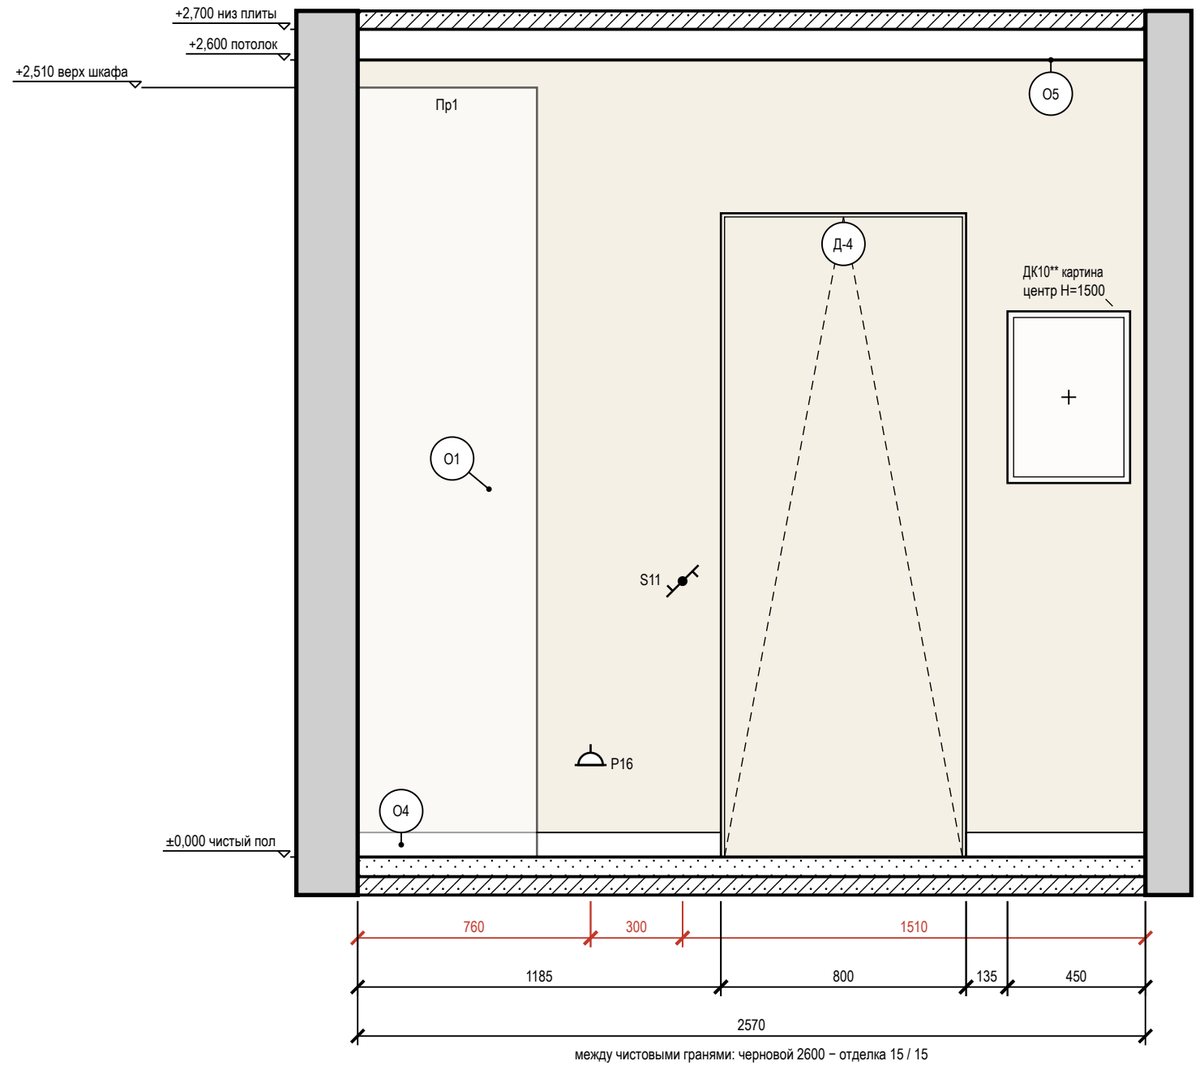

между чистовыми гранями: черновой 2600 − отделка 15 / 15

Ведомость точек и выводов

Марка	Что это	Гр.	Н, мм	От угла, мм	Примечание
Р16	розетка: уборка	6	300	760	
S11	выключатель	2	900	1060	


Условные обозначения

- розетка с заземляющим контактом; у знака — марка, ×N постов в рамке, гр. — группа щита, Н — высота оси, мм
- выключатель одноклавишный
- выключатель с проходной или перекрёстной клавишей (обратный флажок); тип клавиши — в подписи
- привязки точек и выводов от угла и от пола, мм
- мебель и приборы — фасад по расстановке (условно)
- картина (декор): марка Д, крест — центр, Н — высота центра, мм
- дверь скрытого монтажа: полотно в плоскости стены (узел — на листе узлов)
- стены и перекрытия в сечении
- окраска: тон — цвет по коду производителя (условно)
- О1 — марка отделки по реестру отделки альбома
- А — марка развёртки: буква стены, стрелка — взгляд

Ведомость отделки (на листе)

Марка	Поверхность	Материал, изделие	Цвет, код	Кол.
О1	стены	окраска, Tikkurila Euro Power 7, колеровка по NCS, матовая, подготовка Q3	NCS S 0804-Y30R «S 0804-Y30R»	5 м²
О4	плинтус	плинтус МДФ, h 80 мм, аналог: плинтус МДФ под покраску 80×16	NCS S 0804-Y30R «S 0804-Y30R»	1,8 м
О5	потолок	окраска, Tikkurila Euro Power 7, глубокоматовая, подготовка Q3	Tikkurila F485 «Damask»	8,6 м²

Схема развёрток (М 1:50)

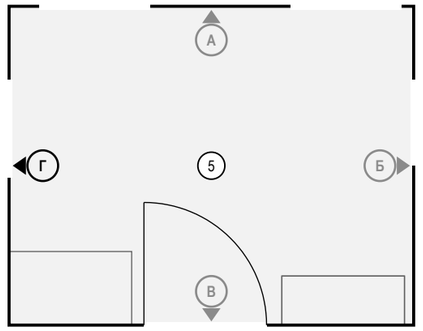

Примечания

1. Развёртки — вид на стену изнутри помещения, по часовой стрелке; расположение — на схеме листа и на листе 83; размеры — в мм по чистовым поверхностям; отметки — в м от ±0,000; высоты Н — от чистого пола помещения до оси изделия, у декора — до центра.
2. Красная цепочка — привязки электроточек и выводов по осям от угла чистовых стен; высота Н — у знака, от чистого пола до оси; высоты мебели, проёмов и границ отделки — колонкой отметок слева. У знака — короткая марка; назначение, группа щита, высота и привязка каждой точки и вывода — в «Ведомости точек и выводов» под видами (каждая точка — строка).
3. У знака электроточки: марка (Р — розетка, S — выключатель, Св — светильник, ЭВ — вывод кабеля), ×N — число постов в рамке, гр. — группа щита, Н — высота оси от чистого пола, мм; группы по клавишам выключателя — на листе выключателей.
4. Схема мебели, приборов и декора не является технической документацией для производства мебели; габариты — по паспортам изделий.
5. Картины и зеркала крепить к основанию по паспорту изделия (закладные и анкеры — в перечне скрытых работ); крест — ось центра предмета.
6. Двери скрытого монтажа — полотно в плоскости стены, отделка стены по полотну, плинтус прерывается у короба (узел — на листе узлов).

Допущения и предложения на листе. Основа листа: размеры помещений и положение проёмов введены заказчиком в брифе, на объекте не замерены (К-1); высота потолка 2700 мм — по брифу заказчика, не замерена (К-2); толщины стен приняты по брифу: наружные 200 мм, внутренние 150 мм — не обмерены (К-1); тип дома монолитный, перекрытие 200 мм — по брифу заказчика, документов нет (К-3); планировка (стены, проёмы, объединение кухни и гостиной, расширение санузла) — по брифу без обмера и плана БТИ (К-7); разрешённая мощность 10 кВт принята, ТУ не переданы (К-8); вентканалы приняты, в брифе не заданы (К-9); подрайон климата не задан — принят не северный (жилые от 2,5 м) (К-10). Знак «*» — принято, не замерено и не подтверждено (замерить на объекте): К-1: дверь пом. 5 (стена В) — входная дверь: положение и ширина проёма — по брифу заказчика, не замерены. Знак «**» — предложение проектировщика, заказчиком не утверждено (согласовать с заказчиком). См. лист открытых вопросов (лист 6, записи К-1–К-3, К-7–К-10; лист 7, запись ИЗ-3).

1000 мм · печать 1:1

Изм.	Кол.уч	Лист	№ док.	Подп.	Дата
Разраб.		Кырлан А.С.			13.11.26
Пров.					
ГИП					
Н. контр.					
Утв.					

ГД-2026-011-АИ

Квартира 56 м²

ЖК «Северный парк», Москва

Дизайн-проект интерьера

Стадия	Лист	Листов
РП	101	119

Развёртка стены Г. Прихожая (пом. 5)

М 1:20

Кырлан Александр Сергеевич


выпуск 13.11.2026 № eb7810814f · стр. 110 из 139

Узлы. Лист 1 из 2

Пороги и стыки покрытий, скрытые двери, короба стояков, гидроизоляция, плинтус

1 Порог 15 мм: мокрая зона — смежное помещение (М 1:5)


Применение: двери Д-5; места — лист 83

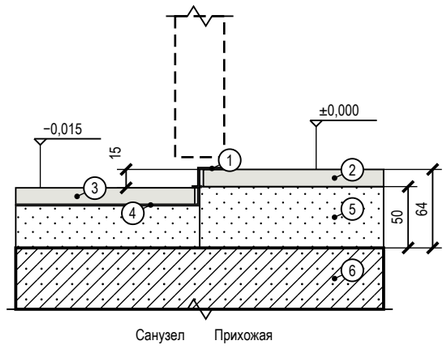

Поз.	Состав слоя, изделие
1	порог-переход металлический, перепад 15 мм, на клей-герметик
2	керамогранит на клею С2 TE S1
3	керамогранит на клею С2 TE S1
4	гидроизоляция в 2 слоя с подъёмом на торец ступени, лента в углу
5	ЦПС М200 50 мм; в мокрой зоне 33 мм
6	плита перекрытия

2 Стык покрытий пола Т-профилем без перепада (М 1:5)

Применение: проёмы 1↔5, 2↔5, 3↔5; места — лист 83

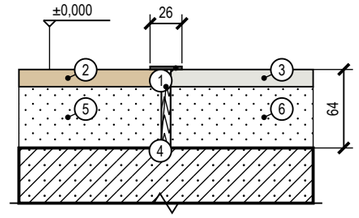

Поз.	Состав слоя, изделие
1	Т-профиль алюминиевый, полка 26 мм, ножка в шов; цвет — по покрытию
2	Гостиная-кухня: инженерная доска на клею
3	Прихожая: керамогранит на клею С2 TE S1
4	шов 8 мм по оси полотна двери, заполнитель эластичный
5	Гостиная-кухня: стяжка ЦПС М200 50 мм
6	Прихожая: стяжка ЦПС М200 50 мм

3 Дверь скрытого монтажа в плоскости стены, плинтус (М 1:5)

Применение: двери Д-2, Д-3, Д-4, Д-5; места — лист 83

Поз.	Состав слоя, изделие
1	плинтус МДФ 80×16 на клей; у короба — зазор 5 мм, окраска в цвет стены
2	полотно 40 мм под окраску, заподлицо со стеной; теневой шов 3 мм
3	стена 150 мм, штукатурка 10 мм с двух сторон
4	короб скрытого монтажа (алюминий), лицом в плоскости отделки; монтаж до штукатурки

4 Короб стояков К1-1 с люком и звукоизоляцией (М 1:10)

Применение: пом. 4; места — лист 83

Поз.	Состав слоя, изделие
1	стены существующие — не ослаблять
2	короб: профиль 27×28, ГКЛВ 2×12,5 мм, облицовка плиткой
3	звукоизоляция стояков рулонная 20 мм; К1-1 Ø110
4	ревизионный люк 300×400 мм нажимной, под плитку; против ревизии стояка

Допущения и предложения на листе

Основа листа: размеры помещений и положение проёмов введены заказчиком в брифе, на объекте не замерены (К-1); высота потолка 2700 мм — по брифу заказчика, не замерена (К-2); толщины стен приняты по брифу: наружные 200 мм, внутренние 150 мм — не обмерены (К-1); тип дома монолитный, перекрытие 200 мм — по брифу заказчика, документов нет (К-3); планировка (стены, проёмы, объединение кухни и гостиной, расширение санузла) — по брифу без обмера и плана БТИ (К-7); разрешённая мощность 10 кВт принята, ТУ не переданы (К-8); вентканалы приняты, в брифе не заданы (К-9); подрайон климата не задан — принят не северный (жилые от 2,5 м) (К-10).

См. лист открытых вопросов (лист 6, записи К-1–К-3, К-7–К-10).

Условные обозначения

- железобетон (плита, стены) — условно: конструкция не установлена
- кладка, перегородка — условно: конструкция не установлена
- стяжка, раствор
- гипсокартон ГКЛВ
- звукоизоляция, эластичный заполнитель
- плитка, керамогранит на клею
- инженерная доска (покрытие пола)
- металлический профиль (порог, Т-профиль, короб двери)
- гидроизоляция (обмазочная, лента)

Примечания

1. Узлы — типовые решения проекта для мест, отмеченных выносками на листе схемы расположения развёрток и узлов; размеры — в мм, отметки — в м от ±0,000.
2. Узлы с гидроизоляцией, закладными и коробами скрытого монтажа принимаются по актам скрытых работ до закрытия отделкой; гидроизоляция — после теста проливом (24 ч).
3. Марки изделий (порог, Т-профиль, короб скрытой двери, люк) — по спецификациям; замена — на аналог с теми же габаритами по согласованию с автором проекта.
4. Материал плиты перекрытия и стен в узлах показан условно (железобетон, кладка): конструкция дома не установлена — крепёж, анкеры и толщины слоёв уточняются после обследования (до него — по допущениям общих указаний).
5. Узлы комплекта выпущены на 2 листах, нумерация узлов сквозная: 1–4 — лист 102 альбома (данный лист); 5–7 — лист 103 альбома.

Изм.	Кол.уч	Лист	№ док.	Подп.	Дата
Разраб.		Кырлан А.С.			13.11.26
Пров.					
ГИП					
Н. контр.					
Утв.					

ГД-2026-011-АИ

Квартира 56 м²

ЖК «Северный парк», Москва

Дизайн-проект интерьера

Стадия	Лист	Листов
РП	102	119

Узлы. Лист 1 из 2

М 1:5; 1:10

Кырлан Александр Сергеевич


выпуск 13.11.2026 № eb7810814f · стр. 111 из 139

Узлы. Лист 2 из 2

Пороги и стыки покрытий, скрытые двери, короба стояков, гидроизоляция, плинтус

5 Гидроизоляция санузла: заход на стены 200 мм, примыкание ванны (М 1:10)


Применение: пом. 4; места — лист 83

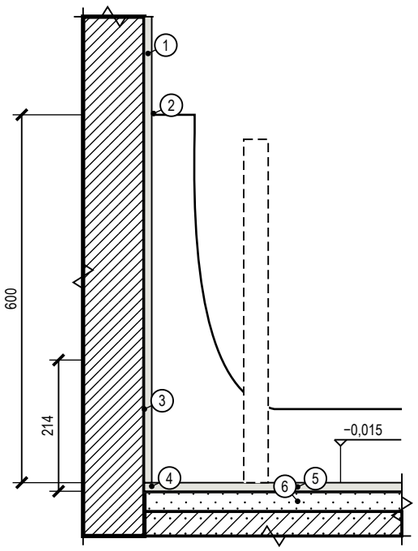

Поз.	Состав слоя, изделие
1	облицовка — плитка на клею C2 TE S1, затирка CG2WA
2	примыкание ванны: лента бордюрная + силиконовый санитарный герметик; облицовка опирается на борт
3	гидроизоляция обмазочная в 2 слоя, заход на стены 200 мм (в зоне душа выше), до облицовки; акт скрытых работ, тест проливом
4	лента гидроизоляционная в углах и у трапов
5	керамогранит на клею C2 TE S1
6	ЦПС М200 33 мм

6 Плинтус МДФ 80×16 мм у окрашенной стены по доске (ламинату) (М 1:5)


Применение: пом. 1, 2, 3; места — лист 83

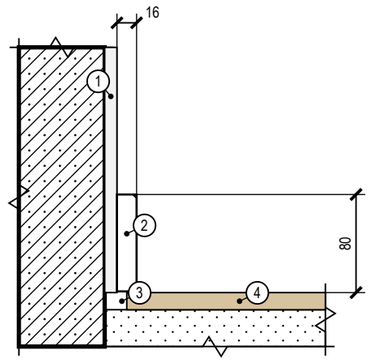

Поз.	Состав слоя, изделие
1	штукатурка, шпаклёвка Q3, окраска — по ведомости отделки
2	плинтус МДФ 80×16 под окраску в цвет стены; клей монтажный — к стене, не к полу
3	зазор покрытия у стены 8–10 мм закрывается плинтусом
4	инженерная доска на клею

7 Плинтус МДФ 80×16 мм у окрашенной стены по керамограниту (плитке) (М 1:5)

Применение: пом. 5; места — лист 83

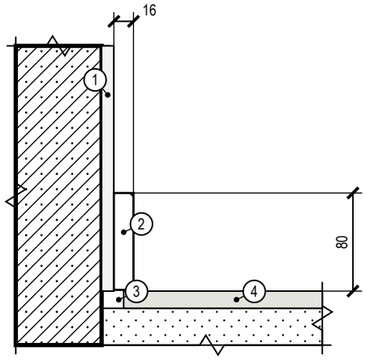

Поз.	Состав слоя, изделие
1	штукатурка, шпаклёвка Q3, окраска — по ведомости отделки
2	плинтус МДФ 80×16 под окраску в цвет стены; клей монтажный — к стене, не к полу
3	зазор покрытия у стены 8–10 мм закрывается плинтусом
4	керамогранит на клею C2 TE S1

Допущения и предложения на листе

Основа листа: размеры помещений и положение проёмов введены заказчиком в брифе, на объекте не замерены (К-1); высота потолка 2700 мм — по брифу заказчика, не замерена (К-2); толщины стен приняты по брифу: наружные 200 мм, внутренние 150 мм — не обмерены (К-1); тип дома монолитный, перекрытие 200 мм — по брифу заказчика, документов нет (К-3); планировка (стены, проёмы, объединение кухни и гостиной, расширение санузла) — по брифу без обмера и плана БТИ (К-7); разрешённая мощность 10 кВт принята, ТУ не переданы (К-8); вентканалы приняты, в брифе не заданы (К-9); подрайон климата не задан — принят не северный (жилые от 2,5 м) (К-10).

См. лист открытых вопросов (лист 6, записи К-1–К-3, К-7–К-10).

Условные обозначения

- железобетон (плита, стены) — условно: конструкция не установлена
- кладка, перегородка — условно: конструкция не установлена
- стяжка, раствор
- плитка, керамогранит на клею
- инженерная доска (покрытие пола)
- гидроизоляция (обмазочная, лента)

Примечания

1. Узлы — типовые решения проекта для мест, отмеченных выносками на листе схемы расположения развёрток и узлов; размеры — в мм, отметки — в м от ±0,000.
2. Узлы с гидроизоляцией, закладными и коробами скрытого монтажа принимаются по актам скрытых работ до закрытия отделкой; гидроизоляция — после теста проливом (24 ч).
3. Марки изделий (порог, Т-профиль, короб скрытой двери, люк) — по спецификациям; замена — на аналог с теми же габаритами по согласованию с автором проекта.
4. Материал плиты перекрытия и стен в узлах показан условно (железобетон, кладка): конструкция дома не установлена — крепёж, анкеры и толщины слоёв уточняются после обследования (до него — по допущениям общих указаний).
5. Узлы комплекта выпущены на 2 листах, нумерация узлов сквозная: 1–4 — лист 102 альбома; 5–7 — лист 103 альбома (данный лист).

Изм.	Кол.уч	Лист	№ док.	Подп.	Дата			
Разраб.		Кырлан А.С.			13.11.26	ГД-2026-011-АИ		
Пров.						Квартира 56 м² ЖК «Северный парк», Москва		
ГИП						Дизайн-проект интерьера	Стадия: РП	Лист: 103 / Листов: 119
Н. контр.						Узлы. Лист 2 из 2 М 1:10; 1:5	Кырлан Александр Сергеевич	
Утв.								

выпуск 13.11.2026 № eb7810814f · стр. 112 из 139

10

Смета

Кырлан Александр Сергеевич

выпуск 13.11.2026 · eb7810814f · стр. 113 из 139

Ведомость объёмов работ

ПРЕДВАРИТЕЛЬНО · не для производства работ · открыто пунктов: 13 (реестр — л. 6, 7)

Объёмы по помещениям от чертежа · площади в м², длины в м · формула, правило проёмов и источник в каждой строке

Ведомость объёмов работ по помещениям

Поз.	Наименование работ (материал, число слоёв)	Ед. изм.	Объём по помещениям (№ по экспликации)					Всего	Формула подсчёта	Правило проёмов	Источник	Цена за ед., ₽	Стоимость, ₽
			1	2	3	4	5						
1. Демонтаж и черновые работы													
1	Демонтаж существующего покрытия пола до основания	м²	20,80	13,60	8,58	4,81	8,58	56,37	S пом.		л. 21, 22	по КП	
2	Демонтаж существующей отделки стен до основания	м²	43,25	32,94	25,79	21,80	21,65	145,43	P × H − проёмы	за вычетом проёмов	л. 21, 22	по КП	
3	Демонтаж существующей отделки потолка до основания	м²	20,80	13,60	8,58	4,81	8,58	56,37	S пом.		л. 21, 22	по КП	
4	Демонтаж существующих дверных блоков	шт	1	1	1	1	1	5	по ведомости проёмов		л. 22, 25	по КП	
5	Демонтаж существующих сантехприборов и электрооборудования (если есть)	компл							по факту на объекте		л. 22	по КП	
6	Кладка перегородки П-1** (блоки, толщина 100 мм): Пеноблок D500, армирование через 2 ряда, штукатурка с двух сторон; предложение, пока П-1** не утверждена автором (К-5)	м²						5,55	2,60 × 2,70 − 1,47 (Д-5 700 × 2100) = 5,55 м², одна сторона; объём 0,56 м³; пом. 4, 5	проёмы вычтены	л. 22	по КП	
7	Кладка перегородки П-3** (кирпич, толщина 120 мм): Кирпич керамический полнотелый, кладка в полкирпича, штукатурка с двух сторон; предложение, пока П-3** не утверждена автором (К-5)	м²						10,80	4,00 × 2,70 = 10,80 м², одна сторона; объём 1,3 м³; пом. 1, 2	проёмы вычтены	л. 22	по КП	
8	Устройство перемычек над проёмами в кладке П-1**; предложение, пока П-1** не утверждена автором (К-5)	шт						1	проём Д-5 700 мм → перемычка 1200 мм (опирание 250 мм с каждой стороны — принято, практика)		л. 22	по КП	
9	Монтаж каркасной перегородки П-2** (С112): каркас ПС усиленный через 600 мм, ГКЛ в 2 слоя с каждой стороны, обрамление проёма профилем УА; предложение, пока П-2** не утверждена автором (К-5)	м²						5,34	2,60 × 2,70 − 1,68 (Д-4 800 × 2100) = 5,34 м², одна сторона; пом. 3, 5	проёмы вычтены	л. 22, 52	2 700	14 418
10	Заполнение каркаса П-2** минераловатной плитой (звукоизоляция, Rw 51 дБ); предложение, пока П-2** не утверждена автором (К-5)	м²						5,34	5,34 м² без проёма		л. 52	по КП	
11	Устройство стяжки: стяжка ЦПС М200, 50 мм	м²	20,87	13,67	8,64	4,86	8,93	56,97	S пом. + S в дверных проёмах (b × t/2)	проёмы добавлены	л. 60, 61	530	30 194
12	Гидроизоляция обмазочная, 2 слоя: пол, стены на 200 мм, зоны замачивания	м²				11,29		11,29	пол + (P − двери) × h заведения + зоны замачивания		л. 57	450	5 081
13	Штукатурка стен по маякам, до 10 мм	м²	43,25	32,94	20,45	21,80	16,31	134,75	P × H − проёмы по обводу коробок − грани перегородок на ГКЛВ	за вычетом проёмов	л. 21, 61	530	71 418
14	Штукатурка оконных откосов шириной до 200 мм	м²	0,62	0,57	0,56			1,75	Σ (2h + b) × глубина откоса	откосы ≤ 200 мм	л. 21	540	945
15	Потолок ГКЛ по каркасу П113, 1 слой	м²	20,80	13,60	8,58	4,81	8,58	56,37	S пом. по плану потолков		л. 53–56	1 500	84 555
Итого по разделу 1 — 206 611 ₽ (позиций 15, из них по КП 9); в сводную смету — л. 110, 111													
2. Инженерные системы													
16	Прокладка кабеля ВВГнг(A)-LS по группам щита: за потолком и в штробах стен (штробы — только после технического заключения, см. строку «Штробы в стенах»)	м						366,20	Σ длин групп щита		л. 37	60	21 972
17	Прокладка слаботочной линии: Кабель домофона — тип по системе поставщика, отдельно от силовых	м						6,70	по лучам от ЩС**: 1 точ., запас 10 %		л. 40	по КП	
18	Прокладка слаботочной линии: Кабель коаксиальный RG-6 (75 Ом) к розеткам ТВ, отдельно от силовых	м						11,70	по лучам от ЩС**: 1 точ., запас 10 %		л. 40	по КП	
19	Прокладка слаботочной линии: Кабель U/UTP кат. 6 (LAN, Wi-Fi и камеры по PoE), отдельно от силовых	м						44,90	по лучам от ЩС**: 5 точ., запас 10 %		л. 40	по КП	
20	Прокладка гофротрубы Ø20 для слаботочных линий, отдельно от силовых	м						57,00	по длине лучей без участков в канале плинтуса (≈ 90 %)		л. 40	140	7 980
21	Сборка слаботочного щита ЩС**: корпус, патч-панель, подключение линий и питания 220 В; коммутатор и точки доступа — оборудование заказчика	шт						1	один щит		л. 35, 36, 40	по КП	
22	Электроточка: подрозетник в бетоне, розетка, выключатель, вывод	шт	26	10	7	4	8	55	по ведомости электроточек		л. 32, 35, 36	950	52 250

Допущения и предложения на листе

Основа листа: размеры помещений и положение проёмов введены заказчиком в брифе, на объекте не замерены (К-1); высота потолка 2700 мм — по брифу заказчика, не замерена (К-2); толщины стен приняты по брифу: наружные 200 мм, внутренние 150 мм — не обмерены (К-1); тип дома монолитный, перекрытие 200 мм — по брифу заказчика, документов нет (К-3); планировка (стены, проёмы, объединение кухни и гостиной, расширение санузла) — по брифу без обмера и плана БТИ (К-7); разрешённая мощность 10 кВт принята, ТУ не переданы (К-8); вентканалы приняты, в брифе не заданы (К-9); подрайон климата не задан — принят не северный (жилые от 2,5 м) (К-10).

Знак «**» — предложение проектировщика, заказчиком не утверждено (согласовать с заказчиком): ЩС — щит слаботочный: место и состав; К-5: П-1 — положение, материал (пеноблок) и толщина 100 мм — по брифу заказчика; конструкция (кладка, армирование, штукатурка) — выбор исполнителя, автором не утверждена; кладка — не ГКЛ: каркас, листы и Rw системы не считаются (система, лист, слои, Rw — «—»); П-2 — положение, материал (ГКЛ) и толщина 150 мм — по брифу заказчика; конструкция (система С112, 2 слоя с каждой стороны, Rw 51 дБ — нижняя граница диапазона системы С112 (51–56 дБ)) — выбор исполнителя, автором не утверждена; П-3 — положение, материал (кирпич) и толщина 120 мм — по брифу заказчика; конструкция (кладка, армирование, штукатурка) — выбор исполнителя, автором не утверждена; кладка — не ГКЛ: каркас, листы и Rw системы не считаются (система, лист, слои, Rw — «—»).

См. лист открытых вопросов (лист 6, записи К-1–К-3, К-5, К-7–К-10).

Изм.	Кол.уч	Лист	№ док.	Подп.	Дата
Разраб.		Кырлан А.С.			13.11.26
Пров.					
ГИП					
Н. контр.					
Утв.					

ГД-2026-011-АИ

Квартира 56 м²

ЖК «Северный парк», Москва

Дизайн-проект интерьера

Стадия	Лист	Листов
РП	104	119

Ведомость объёмов работ

М б/м

Кырлан Александр Сергеевич

Ведомость объёмов работ (продолжение)

Объёмы по помещениям от чертежа · площади в м², длины в м · формула, правило проёмов и источник в каждой строке

Ведомость объёмов работ по помещениям (продолжение)

Поз.	Наименование работ (материал, число слоёв)	Ед. изм.	Объём по помещениям (№ по экспликации)					Всего	Формула подсчёта	Правило проёмов	Источник	Цена за ед., ₽	Стоимость, ₽
			1	2	3	4	5						
23	Штробы в стенах под спуски кабеля к точкам — выполняются только после технического заключения о несущих стенах	м	42,18	18,00	14,00	5,17	11,70	91,05	Σ (H − h) по точкам на стенах: вертикальные спуски	после техзаключения	л. 22, 32	по КП	
24	Установка встраиваемого точечного светильника	шт	12	8	6	3	4	33	по плану освещения		л. 33	750	24 750
25	Монтаж светильника: потолочного, подвесного, настенного	шт	3	2	2	1		8	по плану освещения		л. 33	1 200	9 600
26	Монтаж LED-ленты в алюминиевый профиль	м	9,40	11,70	8,70		1,80	31,60	Σ длин лент по плану освещения		л. 33	230	7 268
27	Установка блока питания LED в доступном месте (люк, шкаф)	шт	2	1	1		1	5	один на LED-группу		л. 33	570	2 850
28	Установка автономного пожарного извещателя	шт	2	1	1		1	5	по плану розеток		л. 32	по КП	
29	Сборка щита: установка автоматов и АВДТ групп, вводного автомата	шт						15	группы + вводной автомат		л. 37	230	3 450
30	Установка вводного УЗО	шт						1	по однолинейной схеме		л. 37	380	380
31	Монтаж инсталляции, установка подвесного унитаза и кнопки смыва	шт				1		1	по плану выводов		л. 43, 50	10 500	10 500
32	Короб инсталляции: каркас и обшивка ГКЛВ в 2 слоя, ревизионный доступ к смыву	шт				1		1	по плану выводов		л. 43, 57–59	по КП	
33	Короб К1 над чистым полом: каркас и обшивка ГКЛВ под плитку (материалы — в спецификации ВК)	м.п.	5,34			3,43		8,77	Σ открытых участков выпусков К1 (профиль листа разводки ВК)		л. 43, 50	по КП	
34	Установка ванны с сифоном	шт				1		1	по плану выводов		л. 43, 50	6 000	6 000
35	Установка умывальника (мойки) с сифоном и смесителем	шт	1			1		2	по плану выводов		л. 43, 50	3 000	6 000
36	Подключение стиральной (посудомоечной) машины к ВК	шт	1			1		2	по плану выводов		л. 43	по КП	
37	Установка радиатора с узлом подключения и терморегулятором	шт	1	1	1			3	по плану отопления		л. 42	по КП	
Итого по разделу 2 — 153 000 ₽ (позиций 22, из них по КП 10); в сводную смету — л. 110, 111													
3. Чистовые работы													
38	Облицовка стен керамогранитом 600×1200 на клею	м²				18,97		18,97	по раскладке: зона облицовки − место за коробом	за вычетом проёмов	л. 57–59	2 500	47 425
39	Облицовка короба инсталляции (ГКЛВ) керамогранитом: лицо, боковины, полка	м²				1,76		1,76	по раскладке: лицо, боковины, полка		л. 57–59	2 500	4 400
40	Облицовка фартука керамогранитом 1200×600	м²	1,82					1,82	по раскладке фартука		л. 57–59, 61	2 400	4 368
41	Укладка керамогранита на пол, 600×600, на клею	м²				4,86	8,93	13,79	S пом. + S в дверных проёмах	проёмы добавлены	л. 57–60	1 800	24 822
42	Затирка швов керамогранита	м²	1,82			25,54	8,58	35,94	Σ S облицовки и пола из плитки		л. 57–59	150	5 391
43	Грунтование стен, 2 слоя (под штукатурку и под отделку)	м²	43,25	32,94	25,79	21,80	21,65	145,43	P × H − проёмы	за вычетом проёмов	л. 61	96	13 961
44	Шпаклёвка стен под окраску, 2 слоя (старт и финиш), уровень Q3	м²	41,43	32,94	25,79		21,65	121,81	P × H − проёмы − фартук	за вычетом проёмов	л. 61	750	91 358
45	Грунтование и шпаклёвка оконных откосов, 2 слоя	м.п.	4,80	4,40	4,30			13,50	Σ (2h + b) по окнам	по окнам	л. 21	300	4 050
46	Грунтование потолка, 2 слоя	м²	20,80	13,60	8,58	4,81	8,58	56,37	S пом.		л. 61	96	5 412
47	Шпаклёвка потолка под окраску, 2 слоя, уровень Q3	м²	20,80	13,60	8,58	4,81	8,58	56,37	S пом.		л. 53–56, 61	950	53 552
48	Окраска потолка водно-дисперсионной краской, 2 слоя	м²	20,80	13,60	8,58	4,81	8,58	56,37	S пом.		л. 61	360	20 293
49	Окраска стен водно-дисперсионной краской, 2 слоя	м²	46,02	32,25	29,50		26,52	134,29	P × H − фартук, проёмы не вычитаются	без вычета проёмов	л. 61	300	40 287
50	Окраска оконных откосов, 2 слоя	м.п.	4,80	4,40	4,30			13,50	Σ (2h + b) по окнам	по окнам	л. 21	120	1 620

Допущения и предложения на листе

Основа листа: размеры помещений и положение проёмов введены заказчиком в брифе, на объекте не замерены (К-1); высота потолка 2700 мм — по брифу заказчика, не замерена (К-2); толщины стен приняты по брифу: наружные 200 мм, внутренние 150 мм — не обмерены (К-1); тип дома монолитный, перекрытие 200 мм — по брифу заказчика, документов нет (К-3); планировка (стены, проёмы, объединение кухни и гостиной, расширение санузла) — по брифу без обмера и плана БТИ (К-7); разрешённая мощность 10 кВт принята, ТУ не переданы (К-8); вентканалы приняты, в брифе не заданы (К-9); подрайон климата не задан — принят не северный (жилые от 2,5 м) (К-10).

См. лист открытых вопросов (лист 6, записи К-1–К-3, К-7–К-10).

Изм.	Кол.уч	Лист	№ док.	Подп.	Дата
Разраб.		Кырлан А.С.			13.11.26
Пров.					
ГИП					
Н. контр.					
Утв.					

ГД-2026-011-АИ

Квартира 56 м²

ЖК «Северный парк», Москва

Дизайн-проект интерьера

Стадия	Лист	Листов
РП	105	119

Ведомость объёмов работ (продолжение)

М б/м

Кырлан Александр Сергеевич

Ведомость объёмов работ (окончание)

ПРЕДВАРИТЕЛЬНО · не для производства работ · открыто пунктов: 13 (реестр — л. 6, 7)

Объёмы по помещениям от чертежа · площади в м², длины в м · формула, правило проёмов и источник в каждой строке

Ведомость объёмов работ по помещениям (продолжение)

Поз.	Наименование работ (материал, число слоёв)	Ед. изм.	Объём по помещениям (№ по экспликации)					Всего	Формула подсчёта	Правило проёмов	Источник	Цена за ед., ₽	Стоимость, ₽
			1	2	3	4	5						
51	Укладка инженерной доски на клей	м²	20,87	13,67	8,64			43,18	S пом. + S в дверных проёмах	проёмы добавлены	л. 60, 61	1 200	51 816
52	Установка плинтуса МДФ h=80 мм	м.п.	17,50	13,90	11,00		7,50	49,90	P − ширина дверных проёмов		л. 61	450	22 455
53	Окраска плинтуса в тоне S 0804-Y30R, 2 слоя	м.п.	17,50	13,90	11,00		7,50	49,90	как плинтус		л. 61	300	14 970
54	Монтаж дверей скрытого монтажа под покраску (поставщик дверей)	шт	1	1	1	1		4	по ведомости проёмов		л. 25	5 250	21 000
55	Входная дверь, поставка с монтажом и откосами	шт						1	по ведомости проёмов		л. 25	по КП	
56	Монтаж телевизора Гс1 на кронштейн, скрытая прокладка HDMI и питания (штроба, трубка), подключение акустики	шт	1					1	по плану расстановки		л. 80	по КП	
Итого по разделу 3 — 427 180 ₽ (позиций 19, из них по КП 2); в сводную смету — л. 110, 111													

Ведомость подсчёта площадей по помещениям

№	Помещение	S пола, м²	P, м	H, м	P × H, м²	Проёмы, м²	Стены нетто, м²	В дверных проёмах, м²	Плинтус, м	Откосы, м.п.
1	Гостиная-кухня	20,80	18,40	2,60	47,84	4,59	43,25	0,07	17,50	4,80
2	Спальня	13,60	14,80	2,50	37,00	4,07	32,94	0,07	13,90	4,40
3	Детская	8,58	11,80	2,50	29,50	3,71	25,79	0,06	11,00	4,30
4	Санузел	4,81	8,90	2,62	23,27	1,47	21,80	0,05	нет	нет
5	Прихожая	8,58	11,80	2,60	30,68	9,03	21,65	0,35	7,50	нет
	Итого	**56,37**			**168,29**	**22,87**	**145,43**	**0,59**	**49,90**	**13,50**

Реестр контрольных сумм

Показатель	По ВОР	По чертежу	Расхождение	Лист
Σ площадей помещений без летних, м² — общая площадь по экспликации	56,37	56,37	0,0 %	л. 21
Стены под окраску, м² (шпаклёвка) ведомость отделки	121,81	121,81	0,0 %	л. 61
Потолки под окраску, м² — ведомость отделки	56,37	56,37	0,0 %	л. 61
Плинтус, м — ведомость отделки	49,90	49,90	0,0 %	л. 61
Плитка к заказу, шт — ведомость плитки	86	86	0,0 %	л. 57
Гидроизоляция, м² — ведомость материалов плитки	11,29	11,29	0,0 %	л. 57
Точки ЭОМ, шт — планы ЭОМ (без щитов)	111	112	-0,9 %	л. 32, 33

Примечания

1. Объёмы — от геометрии проекта (та же, что на планах и в ведомости отделки), не от общей площади: P — периметр чистого контура, H — от чистого пола до низа потолка, проёмы — по наружному обводу коробок.
2. Подсчёт по ГЭСН-2001-15 и ГЭСН-2001-11: штукатурка и шпаклёвка стен — за вычетом проёмов; окраска водными составами — без вычета проёмов (п. 2.24); откосы — отдельно, по ширине до 200 и более 200 мм; полы — с площадью в дверных проёмах.
3. Плитка — по раскладке (целые и с подрезкой); короб инсталляции и фартук — отдельными строками, двойного счёта облицовки нет. Материалы, запас и количество к заказу — в спецификации материалов.
4. Цены — ориентир по открытым прайсам Москвы (прайсы собраны 21.09.2026, часть расценок сверена повторно 06.10.2026 и 08.11.2026), не коммерческое предложение; «по КП» — расценки нет, строка в итог не входит.
5. Демонтаж — по плану демонтажа и общим указаниям: покрытия пола, отделка стен и потолков, дверные блоки — до основания; объёмы справочные — по плану демонтажа (расценки в книге нет — «по КП»).
6. Штробы в стенах — только после технического заключения о несущих стенах (общие указания, план обмера и демонтажа): строка «Штробы в стенах» вертикальные спуски кабеля от потолочной трассы к точкам, объём не меньше фактического (горизонтальные трассы — по исполнительной схеме). Расценки штробления в прайсе нет — «по КП», в итог не входит; кабель в штробах стен прокладывается после неё.
7. Площадь облицовки стен — одно число с тремя названиями: зона облицовки по ведомости отделки 19,93 м² − место за коробом инсталляции 0,96 м² (плитку туда не кладут) = стены под плитку 18,97 м² (строка «Облицовка стен»); облицовка коробов 1,76 м² — отдельной строкой; стены и короба вместе — 20,73 м² (столько плитки по раскладке в спецификации). Источник — один (quantities.js), расхождение на листах ловит.
8. Слаботочные сети: кабель по лучам от ЩС** 63,30 м (U/UTP, RG-6, домофон — по видам), гофра 57,00 м, щит ЩС** с патч-панелью; розетки RJ45 и ТВ монтируются в строке «Электроточка». Длины те же, что в ведомости изделий электрика (одна модель — lowcurrent-engineer/bom.js); оборудование заказчика (точки доступа, камеры, коммутатор) в спецификацию не входит. 2 точ. — предложение листа слаботочки.
9. Перегородки и облицовки ГКЛ (П-2** — 5,34 м²): площадь одной стороны за вычетом проёмов, из той же модели, по которой выпущена схема каркаса; обшивка, профиль и заполнение — в спецификации материалов. П-2** — предложение проектировщика, автором не утверждено: деньги заложены на решение, которое может измениться. Грани перегородок на ГКЛВ вычтены из штукатурки стен (10,68 м²): штукатурят основание, а не обшивку.
10. Перегородки из кладки (П-1** — 5,55 м², 0,56 м³, П-3** — 10,80 м², 1,3 м³): площадь одной стороны за вычетом проёмов, объём — площадь × толщина; перемычки — по одной на проём, длина — ширина + 2 × опирание (принятое опирание 250 мм — практика, СП 15.13330 его не задаёт). Изделия заказываются в м³, кладочная смесь — по ТУ производителя: расхода в источниках нет, число не ставится. Не посчитано: П-1**: размер изделия и толщина шва (masonry.unit, masonry.joint) в данных не заданы — число рядов и длина армирования не считаются; длина одного ряда — 1,9 м; П-1**: штуки изделий не считаются: размер блока в данных не задан — заказ в м³ (объём кладки); П-3**: размер изделия и толщина шва (masonry.unit, masonry.joint) в данных не заданы — число рядов не считается; длина одного ряда — 4 м; П-3**: штуки изделий не считаются: размер кирпича в данных не задан — заказ в м³ (объём кладки). Грани кладки штукатурят — они в строке штукатурки стен помещений. П-1**, П-3** — предложение проектировщика, автором не утверждено.
11. Коробы: стояков (нет) и К1 над чистым полом (8,77 м открытых участков; труба К1 вдоль стен 22,04 м в короб не зашивается — она за приборами, в раме инсталляции и в шахтах). В спецификации ВК короб К1 заказывается с запасом 10 % — 9,70 м. Материалы коробов стояков и инсталляции — в спецификации материалов, К1 — в спецификации ВК.

Допущения и предложения на листе

Основа листа: размеры помещений и положение проёмов введены заказчиком в брифе, на объекте не замерены (К-1); высота потолка 2700 мм — по брифу заказчика, не замерена (К-2); толщины стен приняты по брифу: наружные 200 мм, внутренние 150 мм — не обмерены (К-1); тип дома монолитный, перекрытие 200 мм — по брифу заказчика, документов нет (К-3); планировка (стены, проёмы, объединение кухни и гостиной, расширение санузла) — по брифу без обмера и плана БТИ (К-7); разрешённая мощность 10 кВт принята, ТУ не переданы (К-8); вентканалы приняты, в брифе не заданы (К-9); подрайон климата не задан — принят не северный (жилые от 2,5 м) (К-10).

Знак «**» — предложение проектировщика, заказчиком не утверждено (согласовать с заказчиком): ЩС — щит слаботочный: место и состав; К-5: П-1 — положение, материал (пеноблок) и толщина 100 мм — по брифу заказчика; конструкция (кладка, армирование, штукатурка) — выбор исполнителя, автором не утверждена; кладка — не ГКЛ: каркас, листы и Rw системы не считаются (система, лист, слои, Rw — «—»); П-2 — положение, материал (ГКЛ) и толщина 150 мм — по брифу заказчика; конструкция (система С112, 2 слоя с каждой стороны, Rw 51 дБ — нижняя граница диапазона системы С112 (51–56 дБ)) — выбор исполнителя, автором не утверждена; П-3 — положение, материал (кирпич) и толщина 120 мм — по брифу заказчика; конструкция (кладка, армирование, штукатурка) — выбор исполнителя, автором не утверждена; кладка — не ГКЛ: каркас, листы и Rw системы не считаются (система, лист, слои, Rw — «—»).

См. лист открытых вопросов (лист 6, записи К-1–К-3, К-5, К-7–К-10).

Изм.	Кол.уч	Лист	№ док.	Подп.	Дата	ГД-2026-011-АИ			
						Квартира 56 м²			
						ЖК «Северный парк», Москва			
Разраб.		Кырлан А.С.			13.11.26	Дизайн-проект интерьера	Стадия	Лист	Листов
Пров.							РП	106	119
ГИП									
Н. контр.						Ведомость объёмов работ (окончание)	Кырлан Александр Сергеевич		
Утв.						М б/м			

выпуск 13.11.2026 № eb7810814f · стр. 116 из 139

Спецификация материалов

Отделочные материалы: чистое количество, запас, упаковка, к заказу · ГОСТ 21.110-2013

ПРЕДВАРИТЕЛЬНО · не для производства работ · открыто пунктов: 13 (реестр — л. 6, 7)

Спецификация материалов (ГОСТ 21.110-2013, форма 1)

Поз.	Наименование и техническая характеристика	Тип, марка, артикул	Код продукции	Поставщик	Ед. изм.	Количество				Масса ед., кг	Примечание
						чистое	запас, %	упаковка	к заказу		
Покрытия полов и облицовка											
1	Инженерная доска (дуб натуральный, рабочий слой 4 мм, эмиссия E1, прямая укладка)	1167-1101			м²	43,18	7	по артикулу	46,20 м²		пом. 1, 2, 3; до целой упаковки; л. 60, 61
2	Клей для паркетной и инженерной доски (эластичный, по ТУ изготовителя доски)	по выбору подрядчика			м²	43,18		ведро по ТУ	по ТУ		расход кг/м² — по ТУ клея; л. 60
3	Керамогранит 600×600 мм под травертин	аналог: керамогранит под травертин			шт	15	10	коробка	17 шт		9 целых + 6 с подрезкой; 4,81 м² по раскладке, к заказу 6,12 м²; пом. 4; л. 57–59
4	Керамогранит 600×1200 мм A8UZ	A8UZ			шт	56	10	коробка	63 шт		22 целых + 34 с подрезкой; 29,31 м² по раскладке, к заказу 45,36 м²; пом. 4, 5; л. 57–59
5	Керамогранит 1200×600 мм под травертин, матовый	аналог: керамогранит под травертин, матовый			шт	5	10	коробка	6 шт		0 целых + 5 с подрезкой; 1,82 м² по раскладке, к заказу 4,32 м²; пом. 1; л. 57–59
Сухие смеси и гидроизоляция											
6	Клей плиточный цементный класса C2 TE S1 (ГОСТ Р 56387-2018)	Ceresit CM 17 или аналог			кг	209,32	10	мешок 25 кг	10 меш.	25	слой 5 мм, 1,20 кг/м² на 1 мм; л. 57
7	Затирка цементная класса CG2WA, цвет — по колерной карте	Mapei Ultracolor Plus 132 или аналог			кг	2,62	10	упак. 2 кг	2 упак.	2	расход (a+b)/ab × шов × t × 1,6 кг/м²; л. 57
8	Гидроизоляция обмазочная полимерная, 2 слоя, лента в углах, манжеты на выводах	по выбору подрядчика			м²	11,29	10	ведро по ТУ	по ТУ		пом. 4; расход кг/м² — по ТУ; л. 57
9	Лента демпферная по периметру пола из плитки	по выбору подрядчика			м	15,39	10	рулон	17,00 м		л. 57
10	Смесь цементно-песчаная для стяжки М200 (50 мм, 33 мм)	по выбору подрядчика			м³	2,77	5	мешок по ТУ	по ТУ		S 56,97 м² × толщина; армирование и маяки — по ТУ; л. 60
11	Смесь штукатурная гипсовая для машинного и ручного нанесения по маякам, слой до 10 мм	по выбору подрядчика			м²	134,75	10	мешок по ТУ	по ТУ		пом. 1, 2, 3, 4, 5; расход кг/м² на 1 мм слоя — по ТУ смеси, толщина — по замеру кривизны стен; л. 21, 61
Короба из ГКЛВ											
12	Лист ГКЛВ 12,5 мм, 2500 × 1200 мм, обшивка коробов в 2 слоя	по выбору подрядчика			м²	3,52	10	лист 3,00 м²	2,00 лист		инсталляция пом. 4: 1,76 м²; площадь × 2 слоя; короб К1 над полом — в спецификации ВК; л. 43, 57–59
13	Профиль стальной оцинкованный 27 × 28 мм: каркас коробов (стойки и направляющие)	по выбору подрядчика			м	8,60	10	хлыст 3 м	4 шт		стойки через 400 мм по свободному периметру + направляющие по полу и потолку; крепёж, лента, шпаклёвка швов — по узлу короба; л. 43, 57–59
Перегородки и облицовки из ГКЛВ											
14	Лист ГКЛ 12,5 мм, 2500 × 1200 мм: обшивка перегородок и облицовок, 2 слоя на сторону	по выбору подрядчика			м²	21,36	10	лист 3,00 м²	8,00 лист		П-2**; площадь стороны × 2 слоя × стороны (проёмы вычтены); предложение, пока П-2** не утверждена автором (К-5); л. 22, 52
15	Профиль направляющий ПН 100: по потолку и полу, перемычки над проёмами	по выбору подрядчика			м	5,20	10	хлыст 3 м	2 шт		П-2**; ПН: шаг и положение стоек — на схеме каркаса; длина стойки равна высоте перегородки, стойки режут между направляющими при монтаже; предложение, пока П-2** не утверждена автором (К-5); л. 22, 52
16	Профиль стоечный ПС 100: стойки через шаг каркаса и короткие над проёмами	по выбору подрядчика			м	11,40	10	хлыст 3 м	5 шт		П-2**; ПС: шаг и положение стоек — на схеме каркаса; длина стойки равна высоте перегородки, стойки режут между направляющими при монтаже; предложение, пока П-2** не утверждена автором (К-5); л. 22, 52

Допущения и предложения на листе

Основа листа: размеры помещений и положение проёмов введены заказчиком в брифе, на объекте не замерены (К-1); высота потолка 2700 мм — по брифу заказчика, не замерена (К-2); толщины стен приняты по брифу: наружные 200 мм, внутренние 150 мм — не обмерены (К-1); тип дома монолитный, перекрытие 200 мм — по брифу заказчика, документов нет (К-3); планировка (стены, проёмы, объединение кухни и гостиной, расширение санузла) — по брифу без обмера и плана БТИ (К-7); разрешённая мощность 10 кВт принята, ТУ не переданы (К-8); вентканалы приняты, в брифе не заданы (К-9); подрайон климата не задан — принят не северный (жилые от 2,5 м) (К-10).

Знак «**» — предложение проектировщика, заказчиком не утверждено (согласовать с заказчиком): плинтус пом. 1, 2, 5, фартук пом. 1 — артикул изделия не выбран: позиция описана характеристиками («аналог по характеристикам»), артикул выбирается при закупке; пол пом. 4 — пирог пола: стяжка 33 мм и обмазочная гидроизоляция добавлены разработчиком проекта; артикул изделия не выбран: позиция описана характеристиками («аналог по характеристикам»), артикул выбирается при закупке; К-5: П-2 — положение, материал (ГКЛ) и толщина 150 мм — по брифу заказчика; конструкция (система C112, 2 слоя с каждой стороны, Rw 51 дБ — нижняя граница диапазона системы C112 (51–56 дБ)) — выбор исполнителя, автором не утверждена.

См. лист открытых вопросов (лист 6, записи К-1–К-3, К-5, К-7–К-10).

Изм.	Кол.уч	Лист	№ док.	Подп.	Дата
Разраб.		Кырлан А.С.			13.11.26
Пров.					
ГИП					
Н. контр.					
Утв.					

ГД-2026-011-АИ

Квартира 56 м²

ЖК «Северный парк», Москва

Дизайн-проект интерьера

Стадия	Лист	Листов
РП	107	119

Спецификация материалов

М б/м

Кырлан Александр Сергеевич

Спецификация материалов (продолжение)

Отделочные материалы: чистое количество, запас, упаковка, к заказу · ГОСТ 21.110-2013

Спецификация материалов (ГОСТ 21.110-2013, форма 1) (продолжение)

Поз.	Наименование и техническая характеристика	Тип, марка, артикул	Код продукции	Поставщик	Ед. изм.	Количество				Масса ед., кг	Примечание
						чистое	запас, %	упаковка	к заказу		
17	Профиль усиленный УА 100 (2,0 мм): стойки по краям проёма на полную высоту	по выбору подрядчика			м	5,40	10	хлыст 3 м	2 шт		П-2**; УА: шаг и положение стоек — на схеме каркаса; длина стойки равна высоте перегородки, стойки режут между направляющими при монтаже; предложение, пока П-2** не утверждена автором (К-5); л. 22, 52
18	Плита минераловатная звукопоглощающая в полость каркаса, толщина по глубине профиля 100 мм	по выбору подрядчика			м²	5,34	10	упаковка по ТУ	по ТУ		П-2**; заполнение принято (К-18): марка и плотность — при закупке; Rw системы нормируют с заполнением; предложение, пока П-2** не утверждена автором (К-5); л. 22, 52
19	Лента уплотнительная самоклеящаяся под профили по потолку, полу и у примыканий к стенам	по выбору подрядчика			м	9,80	10	рулон по ТУ	11,00 м		П-2**; по периметру каркаса: потолок, пол без проёма, крайние стойки у примыканий; предложение, пока П-2** не утверждена автором (К-5); л. 22, 52
20	Саморезы для ГКЛ по металлу (по слоям обшивки), дюбели для направляющих — по ТУ изготовителя системы	по выбору подрядчика			м²	21,36		упаковка по ТУ	по ТУ		П-2**; расход шт/м² и шаг дюбелей — по ТУ системы; считаются от площади обшивки; предложение, пока П-2** не утверждена автором (К-5); л. 22, 52
Перегородки из кладки											
21	Пеноблок D500: изделия кладки толщиной 100 мм	по выбору подрядчика			м³	0,56		поддон по ТУ	по ТУ		П-1**; объём кладки 5,55 м² × 100 мм (проёмы вычтены); размер изделия в данных не задан — штуки и запас по ТУ поставщика; предложение, пока П-1** не утверждена автором (К-5); л. 22
22	Смесь кладочная для блоков (клей или раствор — по виду изделия)	по выбору подрядчика			м³ кладки	0,56		мешок по ТУ	по ТУ		П-1**; на 0,56 м³ кладки; количество смеси — по ТУ производителя смеси (расход на м³ кладки; источника расхода в knowledge нет, число не ставится); предложение, пока П-1** не утверждена автором (К-5); л. 22
23	Перемычка над проёмом в кладке П-1**: L 1200 мм	по выбору подрядчика			шт	1		шт	1 шт		П-1**; ширина проёма + 2 × 250 мм опирания (принято, практика: СП 15 опирания не задаёт); тип перемычки — по ТУ изделия; предложение, пока П-1** не утверждена автором (К-5); л. 22
24	Кирпич керамический полнотелый: изделия кладки толщиной 120 мм	по выбору подрядчика			м³	1,30		поддон по ТУ	по ТУ		П-3**; объём кладки 10,8 м² × 120 мм; размер изделия в данных не задан штуки и запас по ТУ поставщика; предложение, пока П-3** не утверждена автором (К-5); л. 22
25	Смесь кладочная для кирпича (клей или раствор — по виду изделия)	по выбору подрядчика			м³ кладки	1,30		мешок по ТУ	по ТУ		П-3**; на 1,3 м³ кладки; количество смеси — по ТУ производителя смеси (расход на м³ кладки; источника расхода в knowledge нет, число не ставится); предложение, пока П-3** не утверждена автором (К-5); л. 22
Слаботочные сети											
26	Кабель домофона — тип по системе поставщика	по выбору подрядчика			м	6,70		бухта по ТУ	7,00 м		по лучам от ЩС**, 1 точ., запас 10 % уже в длине; 2 точ. — предложение листа слаботочки (знак «*» на плане); л. 40
27	Кабель коаксиальный RG-6 (75 Ом) к розеткам ТВ	по выбору подрядчика			м	11,70		бухта по ТУ	12,00 м		по лучам от ЩС**, 1 точ., запас 10 % уже в длине; 2 точ. — предложение листа слаботочки (знак «*» на плане); л. 40
28	Кабель U/UTP кат. 6 (LAN, Wi-Fi и камеры по PoE)	по выбору подрядчика			м	44,90		бухта по ТУ	45,00 м		по лучам от ЩС**, 5 точ., запас 10 % уже в длине; 2 точ. — предложение листа слаботочки (знак «*» на плане); л. 40
29	Гофротруба Ø20 для слаботочных линий, отдельно от силовых	по выбору подрядчика			м	57,00		бухта по ТУ	57,00 м		по длине лучей без участков в канале плинтуса (≈ 90 %); л. 40
30	Розетка компьютерная RJ45, кат. 6, с рамкой и подрозетником	по выбору подрядчика			шт	3		шт	3 шт		LAN1–LAN3; серия механизмов — как у розеток и выключателей; л. 35, 36, 40
31	Розетка телевизионная (коаксиальная) с рамкой и подрозетником	по выбору подрядчика			шт	1		шт	1 шт		ТВ1; серия механизмов — как у розеток и выключателей; л. 35, 36, 40
32	Трубка или монитор домофона (поставка домофонной организации)	по выбору подрядчика			шт	1		шт	1 шт		ДФ1; серия механизмов — как у розеток и выключателей; л. 35, 36, 40

Допущения и предложения на листе

Основа листа: размеры помещений и положение проёмов введены заказчиком в брифе, на объекте не замерены (К-1); высота потолка 2700 мм — по брифу заказчика, не замерена (К-2); толщины стен приняты по брифу: наружные 200 мм, внутренние 150 мм — не обмерены (К-1); тип дома монолитный, перекрытие 200 мм — по брифу заказчика, документов нет (К-3); планировка (стены, проёмы, объединение кухни и гостиной, расширение санузла) — по брифу без обмера и плана БТИ (К-7); разрешённая мощность 10 кВт принята, ТУ не переданы (К-8); вентканалы приняты, в брифе не заданы (К-9); подрайон климата не задан — принят не северный (жилые от 2,5 м) (К-10).

Знак «**» — предложение проектировщика, заказчиком не утверждено (согласовать с заказчиком): ЩС — щит слаботочный: место и состав; плинтус пом. 1, 2, 5, фартук пом. 1 — артикул изделия не выбран: позиция описана характеристиками («аналог по характеристикам»), артикул выбирается при закупке; пол пом. 4 — пирог пола: стяжка 33 мм и обмазочная гидроизоляция добавлены разработчиком проекта; артикул изделия не выбран: позиция описана характеристиками («аналог по характеристикам»), артикул выбирается при закупке; К-5: П-1 — положение, материал (пеноблок) и толщина 100 мм — по брифу заказчика; конструкция (кладка, армирование, штукатурка) — выбор исполнителя, автором не утверждена; кладка — не ГКЛ: каркас, листы и Rw системы не считаются (система, лист, слои, Rw — «—»); П-2 — положение, материал (ГКЛ) и толщина 150 мм — по брифу заказчика; конструкция (система С112, 2 слоя с каждой стороны, Rw 51 дБ — нижняя граница диапазона системы С112 (51–56 дБ)) — выбор исполнителя, автором не утверждена; П-3 — положение, материал (кирпич) и толщина 120 мм — по брифу заказчика; конструкция (кладка, армирование, штукатурка) — выбор исполнителя, автором не утверждена; кладка — не ГКЛ: каркас, листы и Rw системы не считаются (система, лист, слои, Rw — «—»).

См. лист открытых вопросов (лист 6, записи К-1–К-3, К-5, К-7–К-10).

Изм.	Кол.уч	Лист	№ док.	Подп.	Дата			
Разраб.		Кырлан А.С.			13.11.26	ГД-2026-011-АИ		
Пров.						Квартира 56 м² ЖК «Северный парк», Москва		
ГИП						Дизайн-проект интерьера	Стадия: РП	Лист: 108 / Листов: 119
Н. контр.						Спецификация материалов (продолжение) М б/м	Кырлан Александр Сергеевич	
Утв.								

выпуск 13.11.2026 № eb7810814f · стр. 118 из 139

Спецификация материалов (окончание)

ПРЕДВАРИТЕЛЬНО · не для производства работ · открыто пунктов: 13 (реестр — л. 6, 7)

Отделочные материалы: чистое количество, запас, упаковка, к заказу · ГОСТ 21.110-2013

Спецификация материалов (ГОСТ 21.110-2013, форма 1) (продолжение)

Поз.	Наименование и техническая характеристика	Тип, марка, артикул	Код продукции	Поставщик	Ед. изм.	Количество				Масса ед., кг	Примечание
						чистое	запас, %	упаковка	к заказу		
33	Щит слаботочный ЩС**: корпус, DIN-рейка, розетки 220 В	по выбору подрядчика			шт	1		шт	1 шт		ЩС**; серия механизмов — как у розеток и выключателей; л. 35, 36, 40
34	Патч-панель, портов не менее 5	по выбору подрядчика			шт	1		шт	1 шт		серия механизмов — как у розеток и выключателей; л. 35, 36, 40
Лакокрасочные материалы											
35	Краска интерьерная акриловая, матовая, класс истирания 1	Farrow & Ball Modern Emulsion No. 298 «Bancha»			л	2,60	10	банка 2,5 л	2 банк		10,82 м² × 2 сл. × 0,12 л/м²; пом. 1; л. 61
36	Краска интерьерная акриловая, матовая, класс истирания 1	Tikkurila Euro Power 7, колеровка по NCS S 0804-Y30R «S 0804-Y30R»			л	21,42	10	банка 2,7 л	9 банк		89,25 м² × 2 сл. × 0,12 л/м²; пом. 1, 2, 3, 5; л. 61
37	Краска интерьерная акриловая, глубокоматовая, класс истирания 2	Tikkurila Euro Power 7 F485 «Damask»			л	12,37	10	банка 2,7 л	6 банк		51,56 м² × 2 сл. × 0,12 л/м²; пом. 1 (пот.), 2 (пот.), 3 (пот.), 5 (пот.); л. 61
38	Краска интерьерная акриловая, матовая, класс истирания 1	Tikkurila Euro Power 7, колеровка по NCS S 5010-G70Y «S 5010-G70Y»			л	1,52	10	банка 2,7 л	1 банк		6,33 м² × 2 сл. × 0,12 л/м²; пом. 2; л. 61
39	Краска интерьерная акриловая, матовая, класс истирания 1	Tikkurila Euro Power 7 X447 «Sea Smoke»			л	1,56	10	банка 2,7 л	1 банк		6,50 м² × 2 сл. × 0,12 л/м²; пом. 3; л. 61
40	Краска интерьерная акриловая, матовая, класс истирания 1	Tikkurila Euro Power 7 F485 «Damask»			л	1,15	10	банка 2,7 л	1 банк		4,81 м² × 2 сл. × 0,12 л/м²; пом. 4 (пот.); л. 61
41	Шпаклёвка финишная полимерная под окраску (стены и потолки, Q3)	по выбору подрядчика			м²	178,18	10	ведро по ТУ	по ТУ		расход кг/м² на слой — по ТУ; л. 61
42	Грунтовка акриловая глубокого проникновения, 2 слоя	по выбору подрядчика			м²	201,80	10	канистра по ТУ	по ТУ		расход л/м² — по ТУ; л. 61
Погонажные изделия и потолки											
43	Плинтус напольный МДФ под покраску, h=80 мм, крепление к стене	аналог: плинтус МДФ под покраску 80×16			м.п.	38,90	10	хлыст 2,4 м	18 шт		пом. 1, 2, 5; длина хлыста — по артикулу; л. 61
44	Плинтус напольный МДФ под покраску, h=69 мм, крепление к стене	SX165			м.п.	11,00	10	хлыст 2,4 м	6 шт		пом. 3; длина хлыста — по артикулу; л. 61
45	Потолок подвесной ГКЛ/ГКЛВ по каркасу Knauf П113: листы, профили, подвесы, лента, шпаклёвка швов	Knauf П113			м²	56,37		комплект	по л. потолков		площадь — по ведомости потолков; число листов, профилей и подвесов — по шагам каркаса на листе потолков; л. 53–56

Примечания

1. Чистое количество — из ведомости объёмов работ и раскладки плитки; запас — отдельной графой (доска — по ведомости отделки, плитка, краска и плинтус — 10 %); «к заказу» — с запасом и кратно упаковке.
2. Плитка — штуками по раскладке, запас на каждую поверхность. Калибр (рабочий размер) и тон — одной партией на помещение, калибр указать при заказе и сверить с раскладкой до укладки.
3. Краска — 0,12 л/м² на слой (середина вилки 0,10–0,15 л/м²) по фактической площади окраски из ведомости отделки; колеровка одной партией.
4. «По ТУ» — расход задаёт производитель выбранного продукта; количество к заказу — после выбора марки.
5. Поз. 3, 5, 43 заданы характеристиками («аналог:»): марку, артикул и поставщика согласовать с заказчиком до закупки, без артикула не заказывать.
6. Штукатурная смесь — на ту же площадь, что строка ВОР «Штукатурка стен» (134,75 м²): площадь одна, расход смеси задаёт производитель.
7. Коробы инсталляции и стояков: ГКЛВ в 2 слоя и профиль 27 × 28 мм считаются по свободным граням коробов (источник — раскладка плиточника и шахты в данных); короб К1 над полом — в спецификации ВК.
8. Потолки ГКЛ: в этой спецификации — площадь системы П113; число листов, профилей и подвесов — по шагам каркаса на листе потолков (подвесы через 1000, несущие через 500, основные через 1200 мм), схема каркаса не выпущена. Сантехника, светильники и мебель — по своим спецификациям.

Допущения и предложения на листе

Основа листа: размеры помещений и положение проёмов введены заказчиком в брифе, на объекте не замерены (К-1); высота потолка 2700 мм — по брифу заказчика, не замерена (К-2); толщины стен приняты по брифу: наружные 200 мм, внутренние 150 мм — не обмерены (К-1); тип дома монолитный, перекрытие 200 мм — по брифу заказчика, документов нет (К-3); планировка (стены, проёмы, объединение кухни и гостиной, расширение санузла) — по брифу без обмера и плана БТИ (К-7); разрешённая мощность 10 кВт принята, ТУ не переданы (К-8); вентканалы приняты, в брифе не заданы (К-9); подрайон климата не задан — принят не северный (жилые от 2,5 м) (К-10).

Знак «**» — предложение проектировщика, заказчиком не утверждено (согласовать с заказчиком): ЩС — щит слаботочный: место и состав; плинтус пом. 1, 2, 5, фартук пом. 1 — артикул изделия не выбран: позиция описана характеристиками («аналог по характеристикам»), артикул выбирается при закупке; пол пом. 4 — пирог пола: стяжка 33 мм и обмазочная гидроизоляция добавлены разработчиком проекта; артикул изделия не выбран: позиция описана характеристиками («аналог по характеристикам»), артикул выбирается при закупке. См. лист открытых вопросов (лист 6, записи К-1–К-3, К-7–К-10).

Изм.	Кол.уч	Лист	№ док.	Подп.	Дата				
Разраб.		Кырлан А.С.			13.11.26	ГД-2026-011-АИ			
Пров.						Квартира 56 м² ЖК «Северный парк», Москва			
ГИП						Дизайн-проект интерьера	Стадия	Лист	Листов
							РП	109	119
Н. контр.						Спецификация материалов (окончание) М б/м	Кырлан Александр Сергеевич		
Утв.									

Смета ориентировочная

ПРЕДВАРИТЕЛЬНО · не для производства работ · открыто пунктов: 13 (реестр — л. 6, 7)

Работы, материалы, оборудование, услуги и резерв · цены — ориентир по открытым прайсам, не коммерческое предложение

Сводная смета (прайсы собраны 21.09.2026, часть расценок сверена повторно 06.10.2026 и 08.11.2026, Москва)

№	Наименование работ, материалов, услуг	Ед. изм.	Кол-во	Цена за ед., ₽	Стоимость, ₽			Чей подряд	Срок поставки, дн.	Основание	Источник цены
					план	факт	разница				
Работы — по ведомости объёмов работ											
1	Демонтаж и черновые работы (без 9 поз. по КП)	раздел	1		206 611			бригада		ВОР, поз. 1–15; л. 104–106	по ВОР
2	Инженерные системы (без 10 поз. по КП)	раздел	1		153 000			бригада		ВОР, поз. 16–37; л. 104–106	по ВОР
3	Чистовые работы (без 2 поз. по КП)	раздел	1		427 180			бригада, поставщик		ВОР, поз. 38–56; л. 104–106	по ВОР
Материалы — по спецификации материалов											
4	Инженерная доска	м²	46,20	4 513	208 501			поставщик		спецификация, поз. 1	Ц7
5	Керамогранит 600×600 мм	м²	6,12	1 800	11 016			поставщик		спецификация, поз. 3	Ц6
6	Керамогранит 600×1200, 1200×600 мм	м²	49,68	3 500	173 880			поставщик		спецификация, поз. 4, 5	Ц6
7	Клей плиточный цементный класса C2 TE S1	меш.	10	1 800	18 000			поставщик		спецификация, поз. 6	Ц7
8	Затирка цементная класса CG2WA	упак.	2	1 000	2 000			поставщик		спецификация, поз. 7	Ц7
9	Краска Farrow & Ball Modern Emulsion, банка 2,5 л	банк	2	5 800	11 600			поставщик		спецификация, поз. 35	Ц7
10	Краска Tikkurila (Euro Power 7, колеровка по NCS, Euro Power 7), банка 2,7 л	банк	18	3 510	63 180			поставщик		спецификация, поз. 36, 37, 38, 39, 40	Ц6
11	Плинтус напольный МДФ под покраску	шт	24	368	8 832			поставщик		спецификация, поз. 43, 44	Ц7
12	Прочие материалы с расходом по ТУ (клей для доски, гидроизоляция, демпферная лента, смесь для стяжки, смесь штукатурная гипсовая для машинного и ручного нанесения по маякам, лист гклв 12, профиль стальной оцинкованный 27 × 28 мм: каркас коробов (стойки и направляющие), ГКЛВ перегородок, профиль ПН, профиль ПС, профиль УА, минвата в каркас, лента уплотнительная, крепёж каркаса, изделия кладки, кладочная смесь, перемычки, кабель слаботочки, гофра слаботочки, изделия слаботочки, шпаклёвка, грунтовка, каркас и ГКЛ потолков)	компл	1	по КП				поставщик		спецификация, поз. 2, 8, 9, 10, 11, 12, 13, 14, 15, 16, 17, 18, 19, 20, 21, 22, 23, 24, 25, 26, 27, 28, 29, 30, 31, 32, 33, 34, 41, 42, 45	
Оборудование и мебель — поставка по спецификациям											
13	Кухонный гарнитур по проекту кухни, изготовление и монтаж (4–8 нед.)	компл	1	по КП				поставщик	не задан; ориентир 4–8 нед. от замера	л. 75–77	
14	Двери скрытого монтажа с коробом под покраску, поставка	шт	4	по КП				поставщик	не задан; ориентир ≈ 30 дн.	л. 25	

Допущения и предложения на листе

Основа листа: размеры помещений и положение проёмов введены заказчиком в брифе, на объекте не замерены (К-1); высота потолка 2700 мм — по брифу заказчика, не замерена (К-2); толщины стен приняты по брифу: наружные 200 мм, внутренние 150 мм — не обмерены (К-1); тип дома монолитный, перекрытие 200 мм — по брифу заказчика, документов нет (К-3); планировка (стены, проёмы, объединение кухни и гостиной, расширение санузла) — по брифу без обмера и плана БТИ (К-7); разрешённая мощность 10 кВт принята, ТУ не переданы (К-8); вентканалы приняты, в брифе не заданы (К-9); подрайон климата не задан — принят не северный (жилые от 2,5 м) (К-10).

См. лист открытых вопросов (лист 6, записи К-1–К-3, К-7–К-10).

Изм.	Кол.уч	Лист	№ док.	Подп.	Дата
Разраб.		Кырлан А.С.			13.11.26
Пров.					
ГИП					
Н. контр.					
Утв.					

ГД-2026-011-АИ

Квартира 56 м²

ЖК «Северный парк», Москва

Дизайн-проект интерьера

Стадия	Лист	Листов
РП	110	119

Смета ориентировочная

М б/м

Кырлан Александр Сергеевич

Смета ориентировочная (окончание)

ПРЕДВАРИТЕЛЬНО · не для производства работ · открыто пунктов: 13 (реестр — л. 6, 7)

Работы, материалы, оборудование, услуги и резерв · цены — ориентир по открытым прайсам, не коммерческое предложение

Сводная смета (прайсы собраны 21.09.2026, часть расценок сверена повторно 06.10.2026 и 08.11.2026, Москва) (продолжение)

№	Наименование работ, материалов, услуг	Ед. изм.	Кол-во	Цена за ед., ₽	Стоимость, ₽			Чей подряд	Срок поставки, дн.	Основание	Источник цены
					план	факт	разница				
15	Оборудование заказчика слаботочных сетей: точка доступа wi-fi — 2 шт; коммутатор — 1 шт	компл	1	по КП				заказчик		л. 35, 36	
16	Сантехника, светильники, мебель и предметы интерьера	компл	1	по КП				поставщик		л. 50; л. 51; л. 80; л. 28–31	
Прочие работы и услуги											
17	Вынос и вывоз строительного мусора	м³		по факту				бригада		после демонтажа	
18	Подъём материалов на этаж (лифтом или вручную — по договору)	т		по факту				бригада		по массе поставки	
19	Доставка чистовых материалов, 10 % от поставки			10 %	49 701			поставщик		от суммы материалов	
20	Уборка после ремонта	м²	56,37	по факту				бригада		S квартиры	
	Итого работы				**786 791**						
	Итого материалы				**497 009**						
	Итого прочие услуги				**49 701**						
	Резерв на непредвиденные работы и материалы, 15 %				**200 025**						
	ВСЕГО ориентировочно (без оборудования и позиций по КП)				**1 533 526**						

Примечания

1. Смета ориентировочная, не коммерческое предложение: объёмы — из ведомости объёмов работ и спецификации материалов, цены — нижняя граница открытых прайсов Москвы (прайсы собраны 21.09.2026, часть расценок сверена повторно 06.10.2026 и 08.11.2026); перед договором цены подтвердить у подрядчика и поставщиков.
2. Источники цен: Ц1 — Домашний мастерок: прайс на отделочные работы, 2026; Ц2 — Домашний мастерок: прайс на плиточные работы, 2026; Ц3 Домашний мастерок: прайс на электромонтажные работы, 2026; Ц4 — Профи ремонтник: штукатурно-малярные работы; Ц5 — Profi.ru: укладка керамогранита на стены, Москва 2026; Ц6 — knowledge/spec-materials.md, разд. 1 и 3: ориентир по сегментам; Ц7 — Розница Москвы, 09.2026: Леманa ПРО, KGSnab, официальный дилер Farrow & Ball.
3. Повторная сверка с прайсом: 06.10.2026 — перегородка в 2 слоя с усиленным каркасом; 08.11.2026 — гофра слаботочки с затяжкой; остальные расценки — по прайсам, собранным 21.09.2026.
4. В итог не вошли позиции «по КП» и «по факту»: оборудование и мебель, двери, материалы с расходом по ТУ, вывоз мусора, подъём и уборка.
5. В разделе 1 учтены работы по П-2** — 14 418 ₽ (расценка Ц1 за м² конструкции; П-2** — по расценке «усиленный каркас» 2 700 ₽/м² вместо 1 500 ₽/м²: шаг стоек 400 мм или проём с обрамлением УА): это предложение проектировщика, не утверждённое автором (К-5); если конструкции не будет, строки и материалы к ним снимаются, санузел 2 пересчитывается. Обрамление проёма УА, заполнение, профиль и обшивка — материалы «по ТУ», в итог не входят.
6. Доставка — 10 % от материалов, резерв — 15 % (частный ремонт 10–20 %) отдельными строками, в количествах не спрятаны. Графы «факт» и «разница» заполняются по актам.

Допущения и предложения на листе

Основа листа: размеры помещений и положение проёмов введены заказчиком в брифе, на объекте не замерены (К-1); высота потолка 2700 мм — по брифу заказчика, не замерена (К-2); толщины стен приняты по брифу: наружные 200 мм, внутренние 150 мм — не обмерены (К-1); тип дома монолитный, перекрытие 200 мм — по брифу заказчика, документов нет (К-3); планировка (стены, проёмы, объединение кухни и гостиной, расширение санузла) — по брифу без обмера и плана БТИ (К-7); разрешённая мощность 10 кВт принята, ТУ не переданы (К-8); вентканалы приняты, в брифе не заданы (К-9); подрайон климата не задан — принят не северный (жилые от 2,5 м) (К-10).

Знак «**» — предложение проектировщика, заказчиком не утверждено (согласовать с заказчиком): К-5: П-2 — положение, материал (ГКЛ) и толщина 150 мм — по брифу заказчика; конструкция (система С112, 2 слоя с каждой стороны, Rw 51 дБ — нижняя граница диапазона системы С112 (51–56 дБ)) — выбор исполнителя, автором не утверждена.

См. лист открытых вопросов (лист 6, записи К-1–К-3, К-5, К-7–К-10).

						ГД-2026-011-АИ		
						Квартира 56 м²		
						ЖК «Северный парк», Москва		
Изм.	Кол.уч	Лист	№ док.	Подп.	Дата			
Разраб.		Кырлан А.С.			13.11.26	Дизайн-проект интерьера	Стадия: РП	Лист: 111 / Листов: 119
Пров.								
ГИП								
						Смета ориентировочная (окончание)	**Кырлан Александр Сергеевич**	
Н. контр.						М б/м		
Утв.								

выпуск 13.11.2026 № eb78108 14f · стр. 121 из 139

Смета проекта: этапы, помещения, итог

Весь проект: ремонт, мебель, свет, техника, декор · вилка «от … до …» · позиции «по КП» посчитаны отдельно · цены — ориентир, не оферта

Смета проекта: весь проект по категориям (прайсы собраны 21.09.2026, часть расценок сверена повторно 06.10.2026 и 08.11.2026)

Категория	Позиций	С ценой	По КП	Сумма по позициям с ценой, ₽
Ремонт: работы	56	35	21	786 791
Ремонт: материалы отделки и черновые	41	14	27	497 009
Электрика: кабель, механизмы, щит	40	0	40	
Сантехника: приборы, трубы, арматура	32	0	32	
Доставка и услуги	4	1	3	49 701
Мебель (включая кухню)	26	0	26	
Свет: светильники и ленты	46	0	46	
Техника	6	0	6	
Декор и текстиль	53	0	53	
ИТОГО по позициям с ценой (цены — нижняя граница открытых прайсов)	**304**	**50**	**254**	**1 333 501**
Резерв на непредвиденные работы и материалы, 15 % от ремонта				200 025
ВЕСЬ ПРОЕКТ — вилка «от … до …», ₽				**1 333 501 … 1 533 526**
Позиции «по КП» — цена не названа, в итог НЕ входят: работы — 21; материалы отделки и черновые — 27; электрика: кабель, механизмы, щит — 40; сантехника: приборы, трубы, арматура — 32; доставка и услуги — 3; мебель (включая кухню) — 26; свет: светильники и ленты — 46; техника — 6; декор и текстиль — 53			**254**	**итог выше на их цену**

По этапам

Этап	Поз.	С ценой	Сумма, ₽
Демонтаж и черновые работы (работы)	15	6	206 611
Инженерные системы (работы)	22	12	153 000
Чистовые работы (работы)	19	17	427 180
Черновые материалы (смеси, ГКЛ, гидроизоляция)	24	2	20 000
Электрика: кабель, механизмы, щит, слаботочка	40	0	
Сантехника: приборы, трубы, арматура	32	0	
Чистовые материалы (отделка, двери)	17	12	477 009
Доставка и услуги	4	1	49 701
Резерв на непредвиденное, 15 %	1	1	200 025
Итого ремонт (с резервом)			**1 533 526**

По помещениям

Помещение	Работы, ₽	Материалы, ₽	Всего, ₽
Общее по объекту (без привязки к помещению)	48 200		48 200
1. Гостиная-кухня	237 473	151 035	388 508
2. Спальня	157 162	85 851	243 013
3. Детская	113 118	57 537	170 655
4. Санузел	131 686	147 575	279 261
5. Прихожая	99 152	55 011	154 163
Доставка и услуги			49 701
Резерв 15 %			200 025
Итого ремонт (с резервом)			**1 533 526**

Работы по этапам с расценками (ориентир)

№	Работа	Ед.	Объём	Расценка, ₽	Сумма, ₽	Расценка	Чей подряд
1. Демонтаж и черновые работы — работы, ориентир по открытым прайсам							
1	Демонтаж существующего покрытия пола до основания	м²	56,37	по КП			бригада
2	Демонтаж существующей отделки стен до основания	м²	145,43	по КП			бригада

Допущения и предложения на листе

Основа листа: размеры помещений и положение проёмов введены заказчиком в брифе, на объекте не замерены (К-1); высота потолка 2700 мм — по брифу заказчика, не замерена (К-2); толщины стен приняты по брифу: наружные 200 мм, внутренние 150 мм — не обмерены (К-1); тип дома монолитный, перекрытие 200 мм — по брифу заказчика, документов нет (К-3); планировка (стены, проёмы, объединение кухни и гостиной, расширение санузла) — по брифу без обмера и плана БТИ (К-7); разрешённая мощность 10 кВт принята, ТУ не переданы (К-8); вентканалы приняты, в брифе не заданы (К-9); подрайон климата не задан — принят не северный (жилые от 2,5 м) (К-10).

См. лист открытых вопросов (лист 6, записи К-1–К-3, К-7–К-10).

Изм.	Кол.уч	Лист	№ док.	Подп.	Дата
Разраб.		Кырлан А.С.			13.11.26
Пров.					
ГИП					
Н. контр.					
Утв.					

ГД-2026-011-АИ

Квартира 56 м²

ЖК «Северный парк», Москва

Дизайн-проект интерьера

Стадия	Лист	Листов
РП	112	119

Смета проекта: этапы, помещения, итог

М б/м

Кырлан Александр Сергеевич

Смета проекта: этапы, помещения, итог (продолжение)

Весь проект: ремонт, мебель, свет, техника, декор · вилка «от … до …» · позиции «по КП» посчитаны отдельно · цены — ориентир, не оферта

Работы по этапам с расценками (ориентир) (продолжение)

№	Работа	Ед.	Объём	Расценка, ₽	Сумма, ₽	Расценка	Чей подряд
3	Демонтаж существующей отделки потолка до основания	м²	56,37	по КП			бригада
4	Демонтаж существующих дверных блоков	шт	5,00	по КП			бригада
5	Демонтаж существующих сантехприборов и электрооборудования (если есть)	компл		по КП			бригада
6	Кладка перегородки П-1** (блоки, толщина 100 мм): Пеноблок D500, армирование через 2 ряда, штукатурка с двух сторон; предложение, пока П-1** не утверждена автором (К-5)	м²	5,55	по КП			бригада
7	Кладка перегородки П-3** (кирпич, толщина 120 мм): Кирпич керамический полнотелый, кладка в полкирпича, штукатурка с двух сторон; предложение, пока П-3** не утверждена автором (К-5)	м²	10,80	по КП			бригада
8	Устройство перемычек над проёмами в кладке П-1**; предложение, пока П-1** не утверждена автором (К-5)	шт	1,00	по КП			бригада
9	Монтаж каркасной перегородки П-2** (С112): каркас ПС усиленный через 600 мм, ГКЛ в 2 слоя с каждой стороны, обрамление проёма профилем УА; предложение, пока П-2** не утверждена автором (К-5)	м²	5,34	2 700	14 418	Ц1	бригада
10	Заполнение каркаса П-2** минераловатной плитой (звукоизоляция, Rw 51 дБ); предложение, пока П-2** не утверждена автором (К-5)	м²	5,34	по КП			бригада
11	Устройство стяжки: стяжка ЦПС М200, 50 мм	м²	56,97	530	30 194	Ц1	бригада
12	Гидроизоляция обмазочная, 2 слоя: пол, стены на 200 мм, зоны замачивания	м²	11,29	450	5 081	Ц1	бригада
13	Штукатурка стен по маякам, до 10 мм	м²	134,75	530	71 418	Ц1	бригада
14	Штукатурка оконных откосов шириной до 200 мм	м²	1,75	540	945	Ц4	бригада
15	Потолок ГКЛ по каркасу П113, 1 слой	м²	56,37	1 500	84 555	Ц1	бригада
2. Инженерные системы — работы, ориентир по открытым прайсам							
16	Прокладка кабеля ВВГнг(А)-LS по группам щита: за потолком и в штробах стен (штробы — только после технического заключения, см. строку «Штробы в стенах»)	м	366,20	60	21 972	Ц3	бригада
17	Прокладка слаботочной линии: Кабель домофона — тип по системе поставщика, отдельно от силовых	м	6,70	по КП			бригада
18	Прокладка слаботочной линии: Кабель коаксиальный RG-6 (75 Ом) к розеткам ТВ, отдельно от силовых	м	11,70	по КП			бригада
19	Прокладка слаботочной линии: Кабель U/UTP кат. 6 (LAN, Wi-Fi и камеры по PoE), отдельно от силовых	м	44,90	по КП			бригада
20	Прокладка гофротрубы Ø20 для слаботочных линий, отдельно от силовых	м	57,00	140	7 980	Ц3	бригада
21	Сборка слаботочного щита ЩС**: корпус, патч-панель, подключение линий и питания 220 В; коммутатор и точки доступа — оборудование заказчика	шт	1,00	по КП			бригада
22	Электроточка: подрозетник в бетоне, розетка, выключатель, вывод	шт	55,00	950	52 250	Ц3	бригада
23	Штробы в стенах под спуски кабеля к точкам — выполняются только после технического заключения о несущих стенах	м	91,05	по КП			бригада
24	Установка встраиваемого точечного светильника	шт	33,00	750	24 750	Ц3	бригада
25	Монтаж светильника: потолочного, подвесного, настенного	шт	8,00	1 200	9 600	Ц3	бригада
26	Монтаж LED-ленты в алюминиевый профиль	м	31,60	230	7 268	Ц3	бригада
27	Установка блока питания LED в доступном месте (люк, шкаф)	шт	5,00	570	2 850	Ц3	бригада
28	Установка автономного пожарного извещателя	шт	5,00	по КП			бригада
29	Сборка щита: установка автоматов и АВДТ групп, вводного автомата	шт	15,00	230	3 450	Ц3	бригада
30	Установка вводного УЗО	шт	1,00	380	380	Ц3	бригада
31	Монтаж инсталляции, установка подвесного унитаза и кнопки смыва	шт	1,00	10 500	10 500	Ц1	бригада
32	Короб инсталляции: каркас и обшивка ГКЛВ в 2 слоя, ревизионный доступ к смыву	шт	1,00	по КП			бригада

Допущения и предложения на листе

Основа листа: размеры помещений и положение проёмов введены заказчиком в брифе, на объекте не замерены (К-1); высота потолка 2700 мм — по брифу заказчика, не замерена (К-2); толщины стен приняты по брифу: наружные 200 мм, внутренние 150 мм — не обмерены (К-1); тип дома монолитный, перекрытие 200 мм — по брифу заказчика, документов нет (К-3); планировка (стены, проёмы, объединение кухни и гостиной, расширение санузла) — по брифу без обмера и плана БТИ (К-7); разрешённая мощность 10 кВт принята, ТУ не переданы (К-8); вентканалы приняты, в брифе не заданы (К-9); подрайон климата не задан — принят не северный (жилые от 2,5 м) (К-10).

Знак «**» — предложение проектировщика, заказчиком не утверждено (согласовать с заказчиком): ЩС — щит слаботочный: место и состав; К-5: П-1 — положение, материал (пеноблок) и толщина 100 мм — по брифу заказчика; конструкция (кладка, армирование, штукатурка) — выбор исполнителя, автором не утверждена; кладка — не ГКЛ: каркас, листы и Rw системы не считаются (система, лист, слои, Rw — «—»); П-2 — положение, материал (ГКЛ) и толщина 150 мм — по брифу заказчика; конструкция (система С112, 2 слоя с каждой стороны, Rw 51 дБ — нижняя граница диапазона системы С112 (51–56 дБ)) — выбор исполнителя, автором не утверждена; П-3 — положение, материал (кирпич) и толщина 120 мм — по брифу заказчика; конструкция (кладка, армирование, штукатурка) — выбор исполнителя, автором не утверждена; кладка — не ГКЛ: каркас, листы и Rw системы не считаются (система, лист, слои, Rw — «—»).

См. лист открытых вопросов (лист 6, записи К-1–К-3, К-5, К-7–К-10).

Изм.	Кол.уч	Лист	№ док.	Подп.	Дата
Разраб.		Кырлан А.С.			13.11.26
Пров.					
ГИП					
Н. контр.					
Утв.					

ГД-2026-011-АИ

Квартира 56 м²

ЖК «Северный парк», Москва

Дизайн-проект интерьера

Стадия	Лист	Листов
РП	113	119

Смета проекта: этапы, помещения, итог (продолжение)

М б/м

Кырлан Александр Сергеевич

Смета проекта: этапы, помещения, итог (окончание)

ПРЕДВАРИТЕЛЬНО · не для производства работ · открыто пунктов: 13 (реестр — л. 6, 7)

Весь проект: ремонт, мебель, свет, техника, декор · вилка «от … до …» · позиции «по КП» посчитаны отдельно · цены — ориентир, не оферта

Работы по этапам с расценками (ориентир) (продолжение)

№	Работа	Ед.	Объём	Расценка, ₽	Сумма, ₽	Расценка	Чей подряд
33	Короб К1 над чистым полом: каркас и обшивка ГКЛВ под плитку (материалы — в спецификации ВК)	м	8,77	по КП			бригада
34	Установка ванны с сифоном	шт	1,00	6 000	6 000	Ц1	бригада
35	Установка умывальника (мойки) с сифоном и смесителем	шт	2,00	3 000	6 000	Ц1	бригада
36	Подключение стиральной (посудомоечной) машины к ВК	шт	2,00	по КП			бригада
37	Установка радиатора с узлом подключения и терморегулятором	шт	3,00	по КП			бригада
3. Чистовые работы — работы, ориентир по открытым прайсам							
38	Облицовка стен керамогранитом 600×1200 на клею	м²	18,97	2 500	47 425	Ц5	бригада
39	Облицовка короба инсталляции (ГКЛВ) керамогранитом: лицо, боковины, полка	м²	1,76	2 500	4 400	Ц5	бригада
40	Облицовка фартука керамогранитом 1200×600	м²	1,82	2 400	4 368	Ц2	бригада
41	Укладка керамогранита на пол, 600×600, на клею	м²	13,79	1 800	24 822	Ц2	бригада
42	Затирка швов керамогранита	м²	35,94	150	5 391	Ц2	бригада
43	Грунтование стен, 2 слоя (под штукатурку и под отделку)	м²	145,43	96	13 961	Ц4	бригада
44	Шпаклёвка стен под окраску, 2 слоя (старт и финиш), уровень Q3	м²	121,81	750	91 358	Ц1	бригада
45	Грунтование и шпаклёвка оконных откосов, 2 слоя	м	13,50	300	4 050	Ц4	бригада
46	Грунтование потолка, 2 слоя	м²	56,37	96	5 412	Ц4	бригада
47	Шпаклёвка потолка под окраску, 2 слоя, уровень Q3	м²	56,37	950	53 552	Ц1	бригада
48	Окраска потолка водно-дисперсионной краской, 2 слоя	м²	56,37	360	20 293	Ц1	бригада
49	Окраска стен водно-дисперсионной краской, 2 слоя	м²	134,29	300	40 287	Ц1	бригада
50	Окраска оконных откосов, 2 слоя	м	13,50	120	1 620	Ц4	бригада
51	Укладка инженерной доски на клей	м²	43,18	1 200	51 816	Ц1	бригада
52	Установка плинтуса МДФ h=80 мм	м	49,90	450	22 455	Ц1	бригада
53	Окраска плинтуса в тоне S 0804-Y30R, 2 слоя	м	49,90	300	14 970	Ц1	бригада
54	Монтаж дверей скрытого монтажа под покраску (поставщик дверей)	шт	4,00	5 250	21 000	Ц1	поставщик
55	Входная дверь, поставка с монтажом и откосами	шт	1,00	по КП			поставщик
56	Монтаж телевизора Гс1 на кронштейн, скрытая прокладка HDMI и питания (штроба, трубка), подключение акустики	шт	1,00	по КП			бригада
4. Прочие работы и услуги — работы, ориентир по открытым прайсам							
57	Кухонный гарнитур по проекту кухни, изготовление и монтаж (4–8 нед.)	компл	1,00	по КП			поставщик
	Итого работы (позиции с расценкой)				**786 791**		

Примечания

1. Итог «ВЕСЬ ПРОЕКТ» — не прогноз, а сумма того, у чего есть цена: ремонт (работы и материалы по смете сметчика), мебель, свет, техника и декор — по ценам из данных проекта. Позиции без цены названы «по КП» (254 шт.) и в итог не входят: пока цена не названа, итог выше напечатанного.
2. Вилка: «от» — сумма по позициям с ценой по нижней границе открытых прайсов (прайсы собраны 21.09.2026, часть расценок сверена повторно 06.10.2026 и 08.11.2026, Москва); «до» — «от» плюс резерв на непредвиденное (15 % от ремонта; частный ремонт 10–20 %).
3. Работы — ориентир по прайсам подрядчиков, не договорная цена: расценку называет бригада после контрольного обмера. Материалы — по «Смете материалов с ценами» (следующий лист).
4. Разбивка по помещениям — доли: общая закупка делится пропорционально площади (длине, числу), по которой считается позиция; работы — по объёму строки в помещении. Сумма по помещениям, по этапам и по категориям одна и та же.
5. Источники расценок и цен: Ц1 — Домашний мастерок: прайс на отделочные работы, 2026; Ц2 — Домашний мастерок: прайс на плиточные работы, 2026; Ц3 — Домашний мастерок: прайс на электромонтажные работы, 2026; Ц4 — Профи ремонтник: штукатурно-малярные работы; Ц5 — Profi.ru: укладка керамогранита на стены, Москва 2026; Ц6 — справочник материалов: ориентир по сегментам; Ц7 — Розница Москвы, 09.2026: Лемана ПРО, KGSnab, официальный дилер Farrow & Ball.
6. Оборудование «по КП» из сметы сметчика (кухня и др.): 1 поз. — в позиции «по КП» мебели и техники.

Допущения и предложения на листе

Основа листа: размеры помещений и положение проёмов введены заказчиком в брифе, на объекте не замерены (К-1); высота потолка 2700 мм — по брифу заказчика, не замерена (К-2); толщины стен приняты по брифу: наружные 200 мм, внутренние 150 мм — не обмерены (К-1); тип дома монолитный, перекрытие 200 мм — по брифу заказчика, документов нет (К-3); планировка (стены, проёмы, объединение кухни и гостиной, расширение санузла) — по брифу без обмера и плана БТИ (К-7); разрешённая мощность 10 кВт принята, ТУ не переданы (К-8); вентканалы приняты, в брифе не заданы (К-9); подрайон климата не задан — принят не северный (жилые от 2,5 м) (К-10).
См. лист открытых вопросов (лист 6, записи К-1–К-3, К-7–К-10).

Изм.	Кол.уч	Лист	№ док.	Подп.	Дата
Разраб.		Кырлан А.С.			13.11.26
Пров.					
ГИП					
Н. контр.					
Утв.					

ГД-2026-011-АИ

Квартира 56 м²

ЖК «Северный парк», Москва

Дизайн-проект интерьера

Стадия	Лист	Листов
РП	114	119

Смета проекта: этапы, помещения, итог (окончание)
М б/м

Кырлан Александр Сергеевич

выпуск 13.11.2026 № eb7810814f · стр. 124 из 139

Смета материалов с ценами

ПРЕДВАРИТЕЛЬНО · не для производства работ · открыто пунктов: 13 (реестр — л. 6, 7)

Все материалы с количеством, запасом, упаковкой, ценой и сроком · цены — ориентир по открытым прайсам, не оферта · работы не входят

Смета материалов с ценами

№	Позиция	Ед.	Нетто	Запас	С запасом	К закупке (упаковка)	Цена за ед., ₽	Сумма, ₽	Заказать заранее	Доп.
Чистовая отделка — позиций 17, с ценой 12, итого 477 009 ₽										
Покрытия полов и облицовка										
1	Инженерная доска (дуб натуральный, рабочий слой 4 мм, эмиссия E1, прямая укладка) — 1167-1101	м²	43,18	7 %	46,20	46,20 м²	4 513 / м²	208 501		8
2	Керамогранит 600×600 мм под травертин — керамогранит под травертин	шт	15	13 %	17	17 шт · коробка	1 800 / м²	11 016		1, 8
3	Керамогранит 600×1200 мм A8UZ	шт	56	13 %	63	63 шт · коробка	3 500 / м²	158 760		8
4	Керамогранит 1200×600 мм под травертин, матовый — керамогранит под травертин, матовый	шт	5	20 %	6	6 шт · коробка	3 500 / м²	15 120		1, 8
Лакокрасочные материалы										
5	Краска интерьерная акриловая, матовая, класс истирания 1 — Farrow & Ball Modern Emulsion No. 298 «Bancha»	л	2,60	10 %	2,86	2 банка · банка 2,5 л	5 800 / банк	11 600		8
6	Краска интерьерная акриловая, матовая, класс истирания 1 — Tikkurila Euro Power 7, колеровка по NCS S 0804-Y30R «S 0804-Y30R»	л	21,42	10 %	23,56	9 банка · банка 2,7 л	3 510 / банк	31 590		8
7	Краска интерьерная акриловая, глубокоматовая, класс истирания 2 — Tikkurila Euro Power 7 F485 «Damask»	л	12,37	10 %	13,61	6 банка · банка 2,7 л	3 510 / банк	21 060		8
8	Краска интерьерная акриловая, матовая, класс истирания 1 — Tikkurila Euro Power 7, колеровка по NCS S 5010-G70Y «S 5010-G70Y»	л	1,52	10 %	1,67	1 банка · банка 2,7 л	3 510 / банк	3 510		8
9	Краска интерьерная акриловая, матовая, класс истирания 1 — Tikkurila Euro Power 7 X447 «Sea Smoke»	л	1,56	10 %	1,72	1 банка · банка 2,7 л	3 510 / банк	3 510		8
10	Краска интерьерная акриловая, матовая, класс истирания 1 — Tikkurila Euro Power 7 F485 «Damask»	л	1,15	10 %	1,26	1 банка · банка 2,7 л	3 510 / банк	3 510		8
Погонажные изделия и потолки										
11	Плинтус напольный МДФ под покраску, h=80 мм, крепление к стене — плинтус МДФ под покраску 80×16	м	38,90	10 %	42,79	18 шт · хлыст 2,4 м	368 / шт	6 624		1, 8
12	Плинтус напольный МДФ под покраску, h=69 мм, крепление к стене — SX165	м	11,00	10 %	12,10	6 шт · хлыст 2,4 м	368 / шт	2 208		8
Двери										
13	Дверь входная Д-1, проём 1000×2100 мм	шт	1		1	1 шт	по запросу			6
14	Дверь скрытого монтажа (короб под покраску) Д-2, проём 900×2100 мм, UNION FILO-60 / INVISIBLE ФИЛО-60, ГРУНТ; ИНВИЗИБЛ | FILO-60, FONDO; INVISIBLE	шт	1		1	1 шт	по запросу		≈ 30 дн.	6, 7
15	Дверь скрытого монтажа (короб под покраску) Д-3, проём 900×2100 мм, UNION FILO-60 / INVISIBLE ФИЛО-60, ГРУНТ; ИНВИЗИБЛ | FILO-60, FONDO; INVISIBLE	шт	1		1	1 шт	по запросу		≈ 30 дн.	6, 7
16	Дверь скрытого монтажа (короб под покраску) Д-4, проём 800×2100 мм, UNION FILO-60 / INVISIBLE ФИЛО-60, ГРУНТ; ИНВИЗИБЛ | FILO-60, FONDO; INVISIBLE	шт	1		1	1 шт	по запросу		≈ 30 дн.	6, 7
17	Дверь скрытого монтажа (короб под покраску) Д-5, проём 700×2100 мм, UNION FILO-60 / INVISIBLE ФИЛО-60, ГРУНТ; ИНВИЗИБЛ | FILO-60, FONDO; INVISIBLE	шт	1		1	1 шт	по запросу		≈ 30 дн.	6, 7
Черновые материалы — позиций 24, с ценой 2, итого 20 000 ₽										
Покрытия полов и облицовка										
18	Клей для паркетной и инженерной доски (эластичный, по ТУ изготовителя доски)	м²	43,18		43,18	фасовка по ТУ изделия	по запросу			2
Сухие смеси и гидроизоляция										
19	Клей плиточный цементный класса C2 TE S1 (ГОСТ Р 56387-2018) — Ceresit CM 17 или аналог	кг	209,32	10 %	230,25	10 мешок · мешок 25 кг	1 800 / меш.	18 000		8
20	Затирка цементная класса CG2WA, цвет — по колерной карте — Mapei Ultracolor Plus 132 или аналог	кг	2,62	10 %	2,88	2 упаковка · упак. 2 кг	1 000 / упак.	2 000		8

Допущения и предложения на листе

Основа листа: размеры помещений и положение проёмов введены заказчиком в брифе, на объекте не замерены (К-1); высота потолка 2700 мм — по брифу заказчика, не замерена (К-2); толщины стен приняты по брифу: наружные 200 мм, внутренние 150 мм — не обмерены (К-1); тип дома монолитный, перекрытие 200 мм — по брифу заказчика, документов нет (К-3); планировка (стены, проёмы, объединение кухни и гостиной, расширение санузла) — по брифу без обмера и плана БТИ (К-7); разрешённая мощность 10 кВт принята, ТУ не переданы (К-8); вентканалы приняты, в брифе не заданы (К-9); подрайон климата не задан — принят не северный (жилые от 2,5 м) (К-10).

Знак «**» — предложение проектировщика, заказчиком не утверждено (согласовать с заказчиком): плинтус пом. 1, 2, 5, фартук пом. 1 — артикул изделия не выбран: позиция описана характеристиками («аналог по характеристикам»), артикул выбирается при закупке; пол пом. 4 — пирог пола: стяжка 33 мм и обмазочная гидроизоляция добавлены разработчиком проекта; артикул изделия не выбран: позиция описана характеристиками («аналог по характеристикам»), артикул выбирается при закупке.

См. лист открытых вопросов (лист 6, записи К-1–К-3, К-7–К-10).

Изм.	Кол.уч	Лист	№ док.	Подп.	Дата
Разраб.		Кырлан А.С.			13.11.26
Пров.					
ГИП					
Н. контр.					
Утв.					

ГД-2026-011-АИ

Квартира 56 м²

ЖК «Северный парк», Москва

Дизайн-проект интерьера

Стадия	Лист	Листов
РП	115	119

Смета материалов с ценами

М б/м

Кырлан Александр Сергеевич

Смета материалов с ценами (продолжение)

Все материалы с количеством, запасом, упаковкой, ценой и сроком · цены — ориентир по открытым прайсам, не оферта · работы не входят

Смета материалов с ценами (продолжение)

№	Позиция	Ед.	Нетто	Запас	С запасом	К закупке (упаковка)	Цена за ед., ₽	Сумма, ₽	Заказать заранее	Доп.
21	Гидроизоляция обмазочная полимерная, 2 слоя, лента в углах, манжеты на выводах	м²	11,29	10 %	12,42	фасовка по ТУ изделия	по запросу			2
22	Лента демпферная по периметру пола из плитки	м	15,39	10 %	16,93	17,00 м	по запросу			
23	Смесь цементно-песчаная для стяжки М200 (50 мм, 33 мм)	м³	2,77	5 %	2,91	фасовка по ТУ изделия	по запросу			2
24	Смесь штукатурная гипсовая для машинного и ручного нанесения по маякам, слой до 10 мм	м²	134,75	10 %	148,23	фасовка по ТУ изделия	по запросу			2
Короба из ГКЛВ										
25	Лист ГКЛВ 12,5 мм, 2500 × 1200 мм, обшивка коробов в 2 слоя	м²	3,52	10 %	3,87	2 лист · лист 3,00 м²	по запросу			
26	Профиль стальной оцинкованный 27 × 28 мм: каркас коробов (стойки и направляющие)	м	8,60	10 %	9,46	4 шт · хлыст 3 м	по запросу			
Перегородки и облицовки из ГКЛВ										
27	Лист ГКЛ 12,5 мм, 2500 × 1200 мм: обшивка перегородок и облицовок, 2 слоя на сторону	м²	21,36	10 %	23,50	8 лист · лист 3,00 м²	по запросу			
28	Профиль направляющий ПН 100: по потолку и полу, перемычки над проёмами	м	5,20	10 %	5,72	2 шт · хлыст 3 м	по запросу			
29	Профиль стоечный ПС 100: стойки через шаг каркаса и короткие над проёмами	м	11,40	10 %	12,54	5 шт · хлыст 3 м	по запросу			
30	Профиль усиленный УА 100 (2,0 мм): стойки по краям проёма на полную высоту	м	5,40	10 %	5,94	2 шт · хлыст 3 м	по запросу			
31	Плита минераловатная звукопоглощающая в полость каркаса, толщина по глубине профиля 100 мм	м²	5,34	10 %	5,87	фасовка по ТУ изделия	по запросу			2
32	Лента уплотнительная самоклеящаяся под профили по потолку, полу и у примыканий к стенам	м	9,80	10 %	10,78	11,00 м	по запросу			
33	Саморезы для ГКЛ по металлу (по слоям обшивки), дюбели для направляющих — по ТУ изготовителя системы	м²	21,36		21,36	фасовка по ТУ изделия	по запросу			2
Перегородки из кладки										
34	Пеноблок D500: изделия кладки толщиной 100 мм	м³	0,56		0,56	фасовка по ТУ изделия	по запросу			2
35	Смесь кладочная для блоков (клей или раствор — по виду изделия)	м³ кладки	0,56		0,56	фасовка по ТУ изделия	по запросу			2
36	Перемычка над проёмом в кладке П-1**: L 1200 мм	шт	1		1	1 шт	по запросу			
37	Кирпич керамический полнотелый: изделия кладки толщиной 120 мм	м³	1,30		1,30	фасовка по ТУ изделия	по запросу			2
38	Смесь кладочная для кирпича (клей или раствор — по виду изделия)	м³ кладки	1,30		1,30	фасовка по ТУ изделия	по запросу			2
Лакокрасочные материалы										
39	Шпаклёвка финишная полимерная под окраску (стены и потолки, Q3)	м²	178,18	10 %	196,00	фасовка по ТУ изделия	по запросу			2
40	Грунтовка акриловая глубокого проникновения, 2 слоя	м²	201,80	10 %	221,98	фасовка по ТУ изделия	по запросу			2
Погонажные изделия и потолки										
41	Потолок подвесной ГКЛ/ГКЛВ по каркасу Knauf П113: листы, профили, подвесы, лента, шпаклёвка швов	м²	56,37		56,37	фасовка по ТУ изделия	по запросу			2
Электрика и слаботочные сети — позиций 40, с ценой 0, итого 0 ₽										
Слаботочные сети										
42	Кабель домофона — тип по системе поставщика	м	6,70		6,70	7,00 м	по запросу			3
43	Кабель коаксиальный RG-6 (75 Ом) к розеткам ТВ	м	11,70		11,70	12,00 м	по запросу			3

Допущения и предложения на листе

Основа листа: размеры помещений и положение проёмов введены заказчиком в брифе, на объекте не замерены (К-1); высота потолка 2700 мм — по брифу заказчика, не замерена (К-2); толщины стен приняты по брифу: наружные 200 мм, внутренние 150 мм — не обмерены (К-1); тип дома монолитный, перекрытие 200 мм — по брифу заказчика, документов нет (К-3); планировка (стены, проёмы, объединение кухни и гостиной, расширение санузла) — по брифу без обмера и плана БТИ (К-7); разрешённая мощность 10 кВт принята, ТУ не переданы (К-8); вентканалы приняты, в брифе не заданы (К-9); подрайон климата не задан — принят не северный (жилые от 2,5 м) (К-10).

Знак «**» — предложение проектировщика, заказчиком не утверждено (согласовать с заказчиком): плинтус пом. 1, 2, 5, фартук пом. 1 — артикул изделия не выбран: позиция описана характеристиками («аналог по характеристикам»), артикул выбирается при закупке; пол пом. 4 — пирог пола: стяжка 33 мм и обмазочная гидроизоляция добавлены разработчиком проекта; артикул изделия не выбран: позиция описана характеристиками («аналог по характеристикам»), артикул выбирается при закупке; К-5: П-1 — положение, материал (пеноблок) и толщина 100 мм — по брифу заказчика; конструкция (кладка, армирование, штукатурка) — выбор исполнителя, автором не утверждена; кладка — не ГКЛ: каркас, листы и Rw системы не считаются (система, лист, слои, Rw — «—»).

См. лист открытых вопросов (лист 6, записи К-1–К-3, К-5, К-7–К-10).

Изм.	Кол.уч	Лист	№ док.	Подп.	Дата
Разраб.		Кырлан А.С.			13.11.26
Пров.					
ГИП					
Н. контр.					
Утв.					

ГД-2026-011-АИ

Квартира 56 м²

ЖК «Северный парк», Москва

Дизайн-проект интерьера

Стадия	Лист	Листов
РП	116	119

Смета материалов с ценами (продолжение)

М б/м

Кырлан Александр Сергеевич

Смета материалов с ценами (продолжение)

Все материалы с количеством, запасом, упаковкой, ценой и сроком · цены — ориентир по открытым прайсам, не оферта · работы не входят

Смета материалов с ценами (продолжение)

№	Позиция	Ед.	Нетто	Запас	С запасом	К закупке (упаковка)	Цена за ед., ₽	Сумма, ₽	Заказать заранее	Доп.
44	Кабель U/UTP кат. 6 (LAN, Wi-Fi и камеры по PoE)	м	44,90		44,90	45,00 м	по запросу			3
45	Гофротруба Ø20 для слаботочных линий, отдельно от силовых	м	57,00		57,00	57,00 м	по запросу			3
46	Розетка компьютерная RJ45, кат. 6, с рамкой и подрозетником	шт	3		3	3 шт	по запросу			
47	Розетка телевизионная (коаксиальная) с рамкой и подрозетником	шт	1		1	1 шт	по запросу			
48	Трубка или монитор домофона (поставка домофонной организации)	шт	1		1	1 шт	по запросу			
49	Щит слаботочный ЩС**: корпус, DIN-рейка, розетки 220 В	шт	1		1	1 шт	по запросу			
50	Патч-панель, портов не менее 5	шт	1		1	1 шт	по запросу			
Электрика: силовая часть										
51	Кабель силовой ВВГнг(А)-LS 3×1,5 мм²	м	163,60		163,60	164,00 м	по запросу			3
52	Кабель силовой ВВГнг(А)-LS 3×2,5 мм²	м	186,10		186,10	187,00 м	по запросу			3
53	Кабель силовой ВВГнг(А)-LS 3×6 мм²	м	16,50		16,50	17,00 м	по запросу			3
Электрика: щит										
54	Автоматический выключатель дифференциального тока (АВДТ) C10 A, 30 мА, тип A	шт	4		4	4 шт	по запросу			4
55	Автоматический выключатель дифференциального тока (АВДТ) C16 A, 30 мА, тип A	шт	9		9	9 шт	по запросу			4
56	Автоматический выключатель дифференциального тока (АВДТ) C32 A, 30 мА, тип A	шт	1		1	1 шт	по запросу			4
57	Корпус щита ЩРВ-П-48, IP41, 48 модулей	шт	1		1	1 шт	по запросу			4
58	Вводной автомат C50, 1P+N	шт	1		1	1 шт	по запросу			4
59	Вводное УЗО-А 63 А, 100 мА (селективное)	шт	1		1	1 шт	по запросу			4
60	УЗИП тип 2	шт	1		1	1 шт	по запросу			4
Электрика: механизмы и изделия										
61	Розетка с з/к и защитными шторками, 16 А	шт	34		34	34 шт	по запросу			4
62	Розетка IP44 с крышкой, 16 А	шт	2		2	2 шт	по запросу			4
63	Выключатель 1-клав.	шт	1		1	1 шт	по запросу			4
64	Выключатель 1-клав. проходной	шт	1		1	1 шт	по запросу			4
65	Выключатель 2-клав.	шт	1		1	1 шт	по запросу			4
66	Выключатель 2-клав. (перекрёстная + проходная)	шт	1		1	1 шт	по запросу			4
67	Выключатель 2-клав. (проходная + обычная)	шт	4		4	4 шт	по запросу			4
68	Выключатель 2-клав. проходной	шт	1		1	1 шт	по запросу			4
69	Светорегулятор 1-канальный, задний фронт (LED)	шт	4		4	4 шт	по запросу			4
70	Датчик движения ночной подсветки	шт	1		1	1 шт	по запросу			4
71	Рамка 1-постовая	шт	37		37	37 шт	по запросу			4

Допущения и предложения на листе

Основа листа: размеры помещений и положение проёмов введены заказчиком в брифе, на объекте не замерены (К-1); высота потолка 2700 мм — по брифу заказчика, не замерена (К-2); толщины стен приняты по брифу: наружные 200 мм, внутренние 150 мм — не обмерены (К-1); тип дома монолитный, перекрытие 200 мм — по брифу заказчика, документов нет (К-3); планировка (стены, проёмы, объединение кухни и гостиной, расширение санузла) — по брифу без обмера и плана БТИ (К-7); разрешённая мощность 10 кВт принята, ТУ не переданы (К-8); вентканалы приняты, в брифе не заданы (К-9); подрайон климата не задан — принят не северный (жилые от 2,5 м) (К-10).

Знак «**» — предложение проектировщика, заказчиком не утверждено (согласовать с заказчиком): ЩС — щит слаботочный: место и состав; плинтус пом. 1, 2, 5, фартук пом. 1 — артикул изделия не выбран: позиция описана характеристиками («аналог по характеристикам»), артикул выбирается при закупке; пол пом. 4 — пирог пола: стяжка 33 мм и обмазочная гидроизоляция добавлены разработчиком проекта; артикул изделия не выбран: позиция описана характеристиками («аналог по характеристикам»), артикул выбирается при закупке.

См. лист открытых вопросов (лист 6, записи К-1–К-3, К-7–К-10).

Изм.	Кол.уч	Лист	№ док.	Подп.	Дата
Разраб.		Кырлан А.С.			13.11.26
Пров.					
ГИП					
Н. контр.					
Утв.					

ГД-2026-011-АИ

Квартира 56 м²

ЖК «Северный парк», Москва

Дизайн-проект интерьера

Стадия	Лист	Листов
РП	117	119

Смета материалов с ценами (продолжение)

М б/м

Кырлан Александр Сергеевич

Смета материалов с ценами (продолжение)

Все материалы с количеством, запасом, упаковкой, ценой и сроком · цены — ориентир по открытым прайсам, не оферта · работы не входят

Смета материалов с ценами (продолжение)

№	Позиция	Ед.	Нетто	Запас	С запасом	К закупке (упаковка)	Цена за ед., ₽	Сумма, ₽	Заказать заранее	Доп.
72	Рамка 2-постовая	шт	6		6	6 шт	по запросу			4
73	Коробка установочная (подрозетник) Ø68	шт	49		49	49 шт	по запросу			4
74	Вывод кабеля под прибор (клеммник)	шт	5		5	5 шт	по запросу			4
75	Коробка уравнивания потенциалов КУП	шт	1		1	1 шт	по запросу			4
76	Блок питания LED 24 В, 300 Вт, дим.	шт	1		1	1 шт	по запросу			4
77	Блок питания LED 24 В, 60 Вт, дим.	шт	1		1	1 шт	по запросу			4
78	Блок питания LED 24 В, 200 Вт, дим.	шт	2		2	2 шт	по запросу			4
79	Блок питания LED 24 В, 20 Вт	шт	1		1	1 шт	по запросу			4
80	Извещатель дымовой автономный	шт	3		3	3 шт	по запросу			4
81	Извещатель тепловой	шт	2		2	2 шт	по запросу			4
Сантехника — позиций 32, с ценой 0, итого 0 ₽										
Сантехника: санитарные приборы										
82	Ванна встраиваемая акриловая 1700×750 мм, с каркасом, экраном и отверстием слив-перелив — акриловая 1700×750, смеситель настенный	шт	1		1	1 шт	по запросу			5
83	Унитаз подвесной безободковый, с сиденьем микролифт, крепёж и звукоизолирующая прокладка — Laufen Pro 8.2096.6.000.000.1	шт	1		1	1 шт	по запросу			5
84	Инсталляция для подвесного унитаза: рама высотой 1120 мм, бачок, клавиша смыва (ось клавиши 1050 мм от чистого пола)	шт	1		1	1 шт	по запросу			5, 1
85	Раковина над стиральной машиной 600×450 мм, плоская, с переливом и выпуском под плоский сифон	шт	1		1	1 шт	по запросу			5, 1
86	Мойка врезная, нержавеющая сталь, чёрная 700×480 мм, с переливом	шт	1		1	1 шт	по запросу			5, 1
87	Полотенцесушитель электрический, IP44, с терморегулятором	шт	1		1	1 шт	по запросу			5, 1
Сантехника: смесители, сифоны и арматура приборов										
88	Смеситель для ванны настенный однорычажный, межосевое 150 мм, с душевым набором (лейка, шланг, держатель)	шт	1		1	1 шт	по запросу			5, 1
89	Смеситель для умывальника однорычажный, с донным клапаном	шт	1		1	1 шт	по запросу			5, 1
90	Смеситель кухонный однорычажный, высокий излив	шт	1		1	1 шт	по запросу			5, 1
91	Обвязка ванны слив-перелив Ø40/50 с сифоном	шт	1		1	1 шт	по запросу			5, 1
92	Сифон плоский для раковины над стиральной машиной Ø32/40–50, выпуск в стену над корпусом машины	шт	1		1	1 шт	по запросу			5, 1
93	Сифон для мойки с отводом для ПММ Ø40/50	шт	1		1	1 шт	по запросу			5, 1
94	Сифон для стиральной машины встраиваемый в стену Ø50, с обратным клапаном	шт	1		1	1 шт	по запросу			5, 1
95	Кран угловой ½"×½" с гибкой подводкой 40 см (умывальники, мойка)	шт	4		4	4 шт	по запросу			5, 1
96	Кран шаровой угловой ½"×¾" для подключения стиральной и посудомоечной машины	шт	2		2	2 шт	по запросу			5, 1
Сантехника: трубопроводы										
97	Труба полипропиленовая PP-R PN20 Ø20×3,4 (B1) — ГОСТ 32415-2013	м	21,50	10 %	21,50	21,50 м	по запросу			5
98	Труба PP-R, армированная стекловолокном, PN20 Ø20×2,8 (T3) — ГОСТ 32415-2013	м	19,00	10 %	19,00	19,00 м	по запросу			5

Допущения и предложения на листе

Основа листа: размеры помещений и положение проёмов введены заказчиком в брифе, на объекте не замерены (К-1); высота потолка 2700 мм — по брифу заказчика, не замерена (К-2); толщины стен приняты по брифу: наружные 200 мм, внутренние 150 мм — не обмерены (К-1); тип дома монолитный, перекрытие 200 мм — по брифу заказчика, документов нет (К-3); планировка (стены, проёмы, объединение кухни и гостиной, расширение санузла) — по брифу без обмера и плана БТИ (К-7); разрешённая мощность 10 кВт принята, ТУ не переданы (К-8); вентканалы приняты, в брифе не заданы (К-9); подрайон климата не задан — принят не северный (жилые от 2,5 м) (К-10).

Знак «**» — предложение проектировщика, заказчиком не утверждено (согласовать с заказчиком): плинтус пом. 1, 2, 5, фартук пом. 1 — артикул изделия не выбран: позиция описана характеристиками («аналог по характеристикам»), артикул выбирается при закупке; пол пом. 4 — пирог пола: стяжка 33 мм и обмазочная гидроизоляция добавлены разработчиком проекта; артикул изделия не выбран: позиция описана характеристиками («аналог по характеристикам»), артикул выбирается при закупке.

См. лист открытых вопросов (лист 6, записи К-1–К-3, К-7–К-10).

Изм.	Кол.уч	Лист	№ док.	Подп.	Дата
Разраб.		Кырлан А.С.			13.11.26
Пров.					
ГИП					
Н. контр.					
Утв.					

ГД-2026-011-АИ

Квартира 56 м²

ЖК «Северный парк», Москва

Дизайн-проект интерьера

Стадия	Лист	Листов
РП	118	119

Смета материалов с ценами (продолжение)

М б/м

Кырлан Александр Сергеевич

Смета материалов с ценами (окончание)

ПРЕДВАРИТЕЛЬНО · не для производства работ · открыто пунктов: 13 (реестр — л. 6, 7)

Все материалы с количеством, запасом, упаковкой, ценой и сроком · цены — ориентир по открытым прайсам, не оферта · работы не входят

Смета материалов с ценами (продолжение)

№	Позиция	Ед.	Нетто	Запас	С запасом	К закупке (упаковка)	Цена за ед., ₽	Сумма, ₽	Заказать заранее	Доп.
99	Труба канализационная ПП Ø50 (К1) — ГОСТ 32414-2013	м	24,00	10 %	24,00	24,00 м	по запросу			5
100	Труба канализационная ПП Ø110 (К1) — ГОСТ 32414-2013	м	1,00	10 %	1,00	1,00 м	по запросу			5
Сантехника: фасонные части и выводы										
101	Отвод канализационный ПП 45° Ø50 — ГОСТ 32414-2013	шт	16		16	16 шт	по запросу			5
102	Отвод канализационный ПП 45° Ø110 — ГОСТ 32414-2013	шт	4		4	4 шт	по запросу			5
103	Тройник канализационный ПП 45° (врезки ветвей) — ГОСТ 32414-2013	шт	4		4	4 шт	по запросу			5
104	Ревизия канализационная ПП (после поворота трассы) — ГОСТ 32414-2013	шт	6		6	6 шт	по запросу			5
105	Фитинги PP-R Ø20: тройники, угольники 90° (ветви и повороты В1, Т3) — ГОСТ 32415-2013	шт	23		23	23 шт	по запросу			5
106	Водорозетка PP-R Ø20×½" настенная, с креплением — ГОСТ 32415-2013	шт	9		9	9 шт	по запросу			5
Сантехника: узлы ввода, люки, короба										
107	Кран шаровой латунный Ду15 PN16 (отключение ввода)	шт	2		2	2 шт	по запросу			5, 1
108	Фильтр сетчатый косой Ду15	шт	2		2	2 шт	по запросу			5, 1
109	Счётчик воды крыльчатый Ду15 (ХВ, ГВ), с поверкой	шт	2		2	2 шт	по запросу			5, 1
110	Клапан обратный Ду15	шт	2		2	2 шт	по запросу			5, 1
111	Люк ревизионный нажимной под плитку 300×400 мм	шт	1		1	1 шт	по запросу			5, 1
112	Звукоизоляция стояка К1 в коробе: рулонный звукоизоляционный материал ≥ 10 мм, обмотка стояка на высоту этажа	м	2,70		2,70	2,70 м	по запросу			5, 1
113	Короб К1 над полом: профиль ПН/ПС, ГКЛВ 12,5 мм под плитку	м	9,70		9,70	9,70 м	по запросу			5, 1
	ИТОГО материалы (позиций с ценой 14 из 113; без цены 99 — «по запросу», в итог не входят)							**497 009**		

Примечания

1. Количества — из единой книги материалов проекта: тот же расход, что в спецификации отделочных материалов, смете и списке покупок. Запас — на подрезку и бой; норма запаса печатается в графе «Запас», её основание — в отдельном документе «Смета на материалы».
2. Цены — нижняя граница открытых прайсов (прайсы собраны 21.09.2026, часть расценок сверена повторно 06.10.2026 и 08.11.2026, Москва); не предложение (оферта) магазинов. Цены нет — «по запросу», позиция в итог не входит. Работы в эту смету не входят (они — на листе «Смета проекта»).
3. Доп. 1. Изделие не выбрано: позиция описана по характеристикам («аналог»); марка, артикул и цена определяются при выборе изделия.
4. Доп. 2. Фасовка не задана в данных: количество дано в мерах расчёта, число упаковок определяется по выбранному продукту (расход и тара — по ТУ).
5. Доп. 3. Длина кабеля — по длинам групп щита из данных электрика; запас на подрезку в длину не заложен — берите бухту с запасом 5–10 %.
6. Доп. 4. Механизмы, рамки и подрозетники — по ведомости изделий электрика; серию механизмов выбирает заказчик.
7. Доп. 5. Трубы и фасонные части — по трассам листа разводки, +10 % на подрезку (уже в количестве); модели приборов заказчик выбирает сам.
8. Доп. 6. Двери: цена и срок называет поставщик после выбора изделия; в смету стоят только если цена задана в данных.
9. Доп. 7. Срок поставки — из данных проекта; если срок не задан, указан типовой диапазон практики как ориентир, а не срок поставщика.
10. Доп. 8. Цена — нижняя граница открытых прайс-листов на дату сбора (книга цен проекта); не коммерческое предложение магазина.
11. Доп. 9. Доли по помещениям справочные: общая закупка делится пропорционально площади (длине, числу), по которой считается позиция.

Допущения и предложения на листе

Основа листа: размеры помещений и положение проёмов введены заказчиком в брифе, на объекте не замерены (К-1); высота потолка 2700 мм — по брифу заказчика, не замерена (К-2); толщины стен приняты по брифу: наружные 200 мм, внутренние 150 мм — не обмерены (К-1); тип дома монолитный, перекрытие 200 мм — по брифу заказчика, документов нет (К-3); планировка (стены, проёмы, объединение кухни и гостиной, расширение санузла) — по брифу без обмера и плана БТИ (К-7); разрешённая мощность 10 кВт принята, ТУ не переданы (К-8); вентканалы приняты, в брифе не заданы (К-9); подрайон климата не задан — принят не северный (жилые от 2,5 м) (К-10).

Знак «**» — предложение проектировщика, заказчиком не утверждено (согласовать с заказчиком): плинтус пом. 1, 2, 5, фартук пом. 1 — артикул изделия не выбран: позиция описана характеристиками («аналог по характеристикам»), артикул выбирается при закупке; пол пом. 4 — пирог пола: стяжка 33 мм и обмазочная гидроизоляция добавлены разработчиком проекта; артикул изделия не выбран: позиция описана характеристиками («аналог по характеристикам»), артикул выбирается при закупке.

См. лист открытых вопросов (лист 6, записи К-1–К-3, К-7–К-10).

Изм.	Кол.уч	Лист	№ док.	Подп.	Дата
Разраб.		Кырлан А.С.			13.11.26
Пров.					
ГИП					
Н. контр.					
Утв.					

ГД-2026-011-АИ

Квартира 56 м²

ЖК «Северный парк», Москва

Дизайн-проект интерьера

Стадия	Лист	Листов
РП	119	119

Смета материалов с ценами (окончание)

М б/м

Кырлан Александр Сергеевич

11

Визуализации

Кырлан Александр Сергеевич


выпуск 13.11.2026 · eb78108314f · стр. 130 из 139



Планировочное решение · вид сверху

Квартира 56 м² · визуализация 1 из 9

выпуск 13.11.2026 № eb78108f4f · стр. 131 из 139

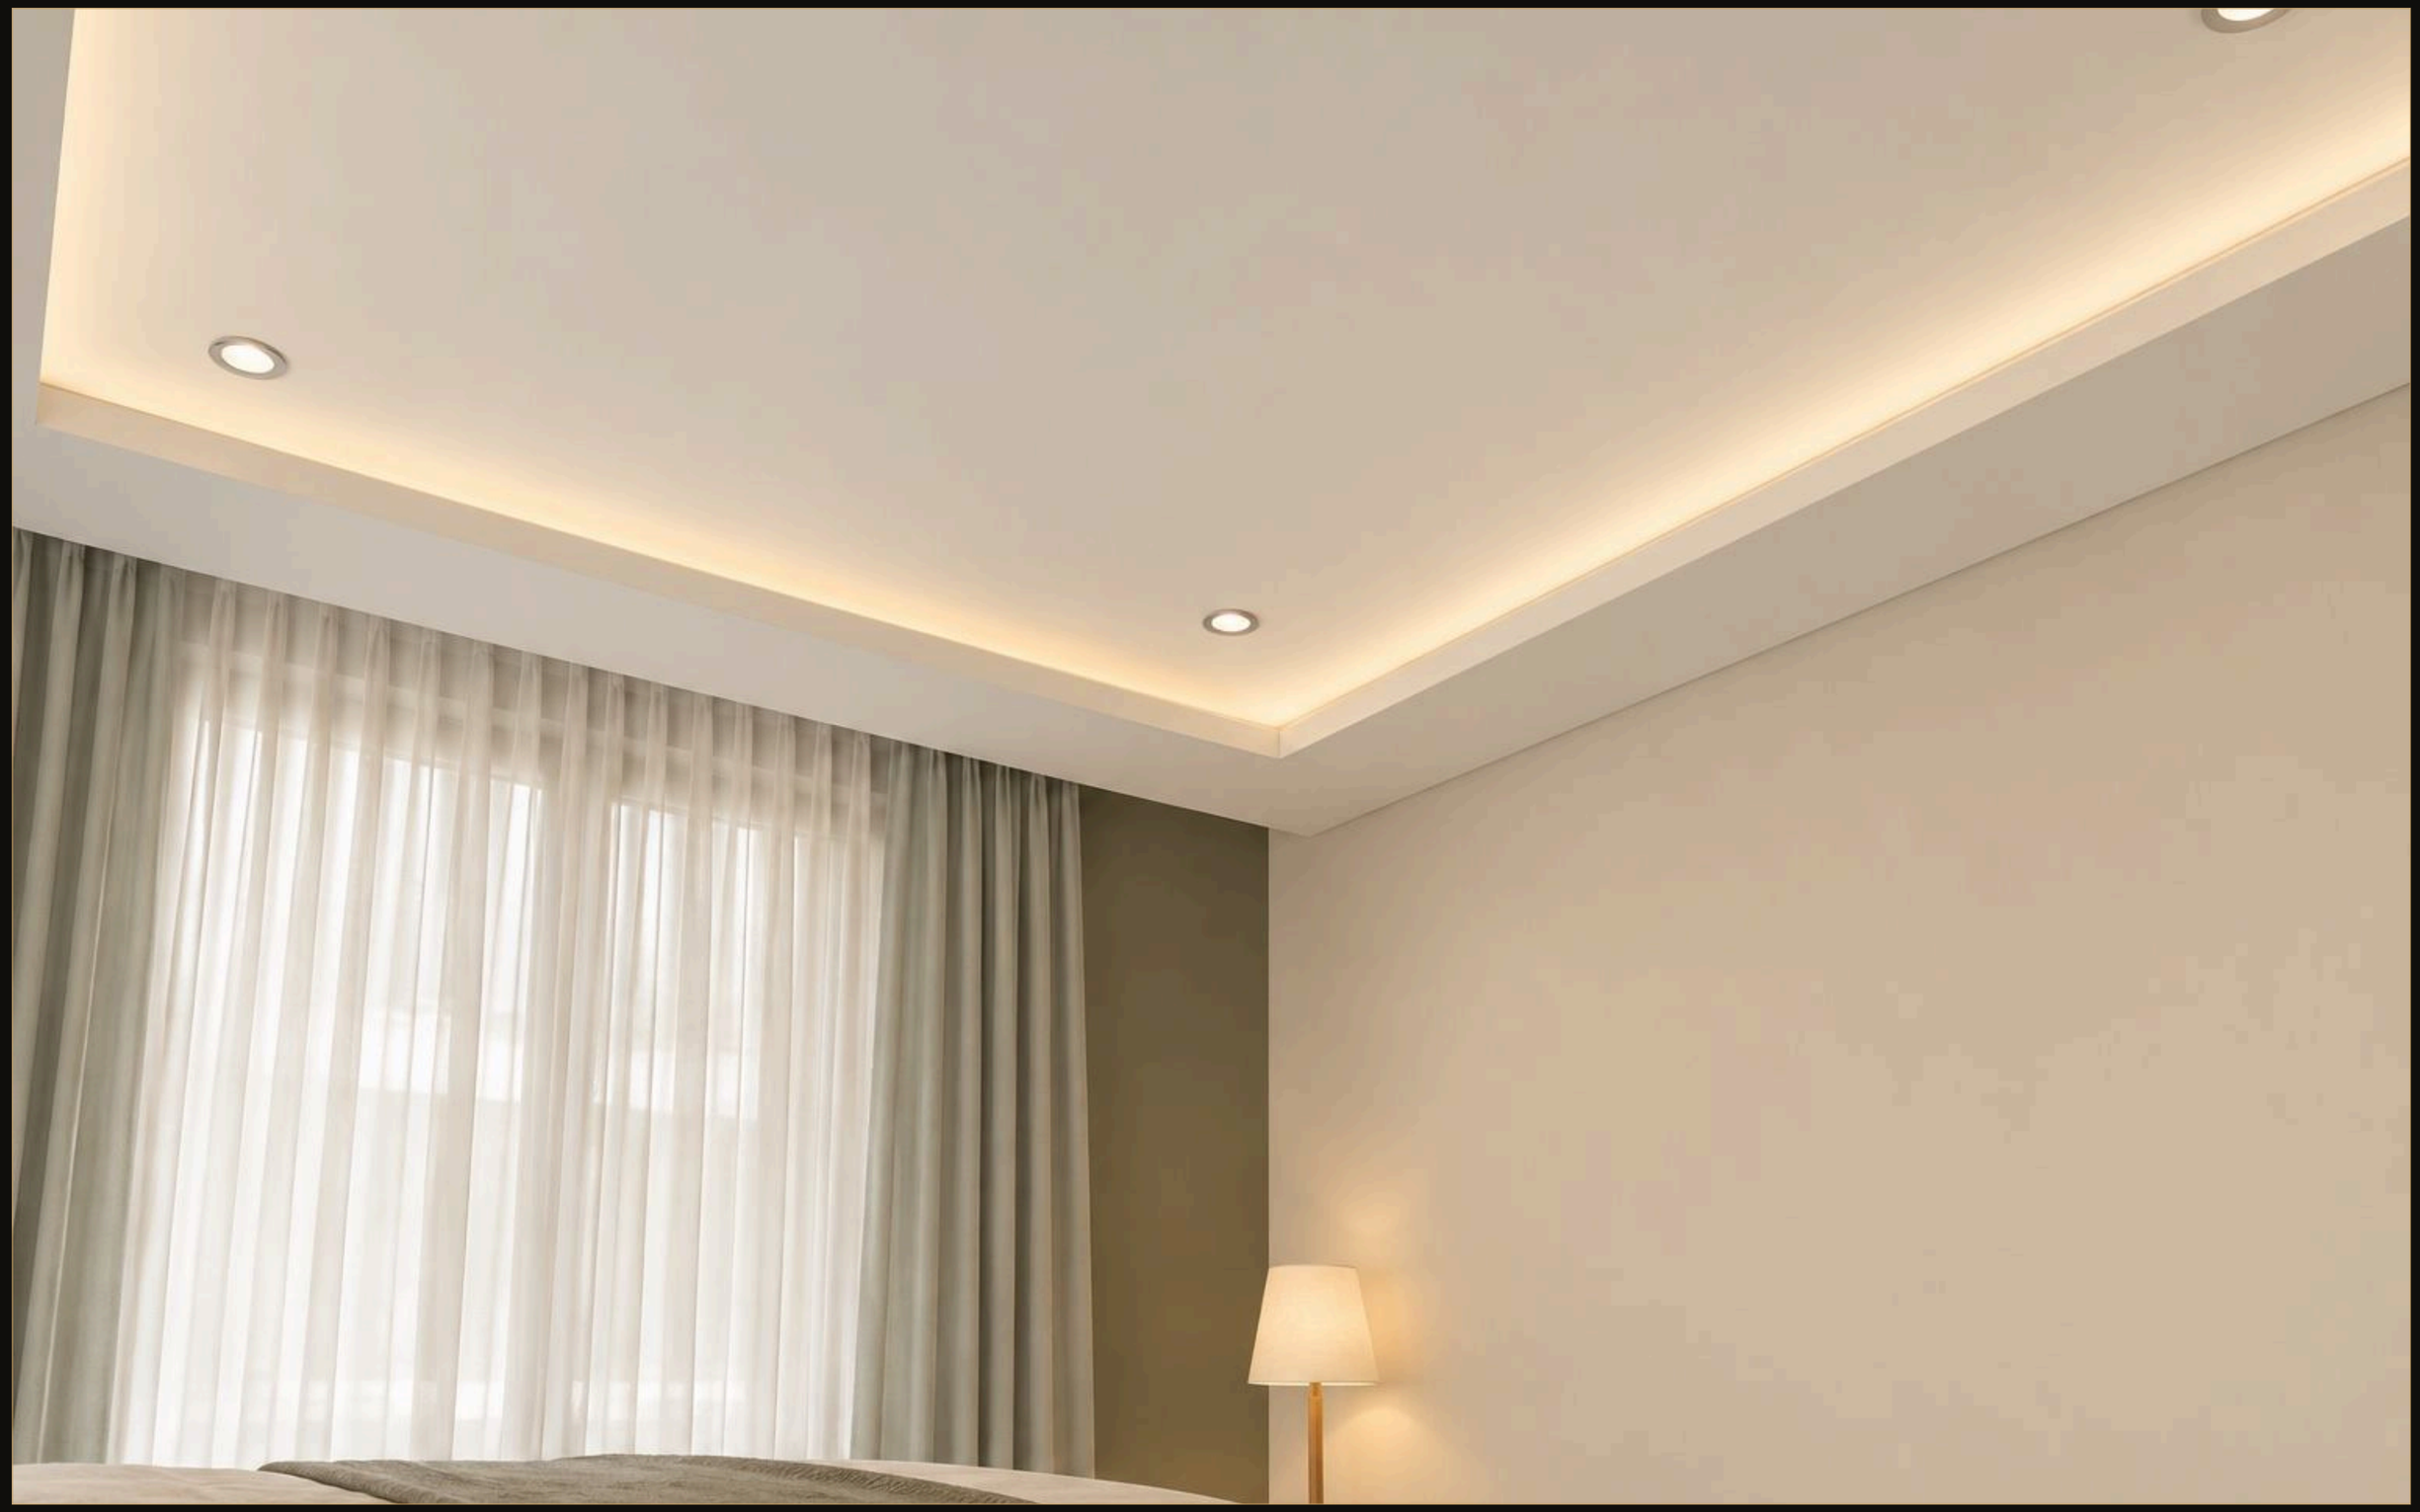

Спальня · потолок

Квартира 56 м² · визуализация 2 из 9

выпуск 13.11.2026 № eb7810814f · стр. 132 из 139



Детская · потолок

Квартира 56 м² · визуализация 3 из 9

выпуск 13.11.2026 № eb7810814f · стр. 133 из 139



Санузел · стена А

Квартира 56 м² · визуализация 4 из 9

выпуск 13.11.2026 № eb7810814f · стр. 134 из 139



Санузел · стена Г

Квартира 56 м² · визуализация 5 из 9

выпуск 13.11.2026 № eb7810814f · стр. 135 из 139



Спальня · стена А

Квартира 56 м² · визуализация 6 из 9

выпуск 13.11.2026 № eb7810814f · стр. 136 из 139

выпуск 13.11.2026 № eb7810814f · стр. 137 из 139



Детская · стена А



Детская · стена Б

Квартира 56 м² · визуализация 8 из 9

выпуск 13.11.2026 № eb7810814f · стр. 138 из 139

выпуск 13.11.2026 № eb7810814f · стр. 139 из 139



Гостиная-кухня · стена B