
LINEA

ДИЗАЙН-ПРОЕКТ ИНТЕРЬЕРА

Квартира 56 м²

ЖК «Северный парк», Москва · джапанди

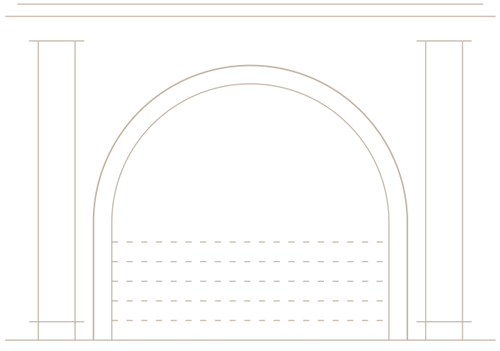

ПАЛИТРА ОТДЕЛКИ

NCS S 0804-Y30	F485	F&B No. 298	X447	NCS S 5010-G70
53 %	33 %	6 %	4 %	4 %

АВТОР ПРОЕКТА

Кырлан Александр Сергеевич

Ноябрь 2026



Визуализация гостиной · 3D

ОБЩАЯ ПЛОЩАДЬ	ПОМЕЩЕНИЙ	СТАДИЯ	ШИФР	ОСНОВА
56,37 м²	5, из них жилых 3	Проект · предварительно	ГД-2026-011-АИ	план заказчика, без обмера

Как оставить правку: кнопка «Правка к этому листу» в правом верхнем углу любого листа · все листы проекта: дизайн-студия-квартир.рф/review.html?p=gost-lineademo

выпуск 13.11.2026 № 568a382a0d · стр. 1 из 92



	Лист	№ док.	Подпись	Дата
Дизайнер	Кырлан А.С.			13.11.26
Проверил				
Н. контр.				
Утв.				

Проект: Квартира 56 м²

Визуализация. Вид сверху	Стадия	Лист	Листов
	П	2	92

Объект

Квартира 56 м²: 56 м², помещений 5, из них жилых 3.

Стиль: джапанди 100 %. Стадия: предварительный альбом без обмера, планировка по плану заказчика.

Открытых вопросов 12, конфликтов разделов 0; изменений утверждено 2, ждут подписи 1.

Розетки и выводы

36 розеток (рамок 30), 5 выводов кабеля под технику и свет, 14 групп щита — всё с высотами от чистого пола: листы 40, 43.

Что решено (подписано вами)

ИЗ-1 — Д-2 — петли у правого откоса, консоль М-15 — смещение 700…2500, кресло М-14 — у 2100…2850: проход от двери к кухне 975 / 825 мм.

ИЗ-2 — Стол М-24 сдвинут вдоль стены Б на 250 мм от двери: у 5800…6400 мм (было 5550…6150), х 2000…3200 прежний.

Предложено, ждёт подписи: ИЗ-3

Что ждёт вашего ответа

вопросов 12; блокируют заказ или работы — 5, они первыми и выделены

№	Вопрос	Варианты · что будет без ответа	Нужен ответ
К-3	Тип дома (монолитный) и толщина перекрытия 200 мм указаны заказчиком в брифе.	Без ответа: все существующие стены считаются несущими; демонтаж и штробление в них не выполняются до технического заключения.	**До начала демонтажных работ**
К-6	Цвета названы заказчиком в брифе словами (тёплый белый, натуральное дерево, серо-зелёный).	Без ответа: коды — предложение исполнителя; краску не закупать до выкрасов.	**до заказа мебели и материалов**
К-7	Планировка принята по брифу заказчика: положение существующих стен и проёмов, объединение кухни с гостиной (демонтаж С-1), расширение санузла (демонтаж С-2, перегородка П-1)…	Без ответа: расстановка остаётся предложением; мебель на заказ (кухня, шкафы) не заказывать.	**до демонтажа**
К-11	Мойка кухонная С-01 (пом. 1 «Гостиная-кухня»), выпуск К1-1 Ø50: до стояка Ст К1-1 15,58 м через пом. 5 «Прихожая», перепад 390 мм — короб 470×110 над полом через чужие…	Решить: (а) насосная установка (КНС) под мойкой/прибором с напорной трубой Ø32 к стояку (по паспорту, обслуживаемый люк); (б) подиум кухонной зоны на 470 мм с трубой под ним; (в) перенос прибора ближе к стояку…	**до начала этих работ**
К-12	Помещение «Спальня»: выключатель основного света L1 (S1) не у входа — у двери Д-3 со стороны ручки свободного места нет (проём в 100 мм от угла, мебель у двери, чужие…	Варианты: (а) петли на другую сторону — ручка уходит от угла, выключатель встаёт у ручки; (б) шкаф или тумбу у двери сдвинуть на 300 мм — место освобождается; (в) беспроводной выключатель на клее у ручки (реле в…	**до выпуска рабочей документации**
К-1	Размеры помещений, толщины стен (наружные 200 мм, перегородки 150 мм) и положение проёмов введены заказчиком в бриф заказчика (site-brief-wizard, 01.08.2026): контрольный обмер…	Без ответа: все размеры альбома остаются по брифу заказчика и не считаются замеренными; заказ изделий по ним не ведётся.	до заказа мебели и материалов
К-2	Высота потолка 2700 мм указана заказчиком в брифе, на объекте не замерена.	Без ответа: вертикальные размеры альбома остаются по брифу и не считаются замеренными.	до выпуска рабочей документации
К-4	Положение и диаметры стояков (канализации, холодной воды) указаны заказчиком в брифе, не замерены.	Без ответа: трассы и привязки выводов остаются по положению стояков из брифа и не считаются замеренными.	до выпуска рабочей документации
К-5	Новые перегородки заданы заказчиком в брифе положением, материалом и толщиной.	Без ответа: конструкция перегородок остаётся по решению исполнителя со знаком «предложено».	до выпуска рабочей документации
К-8	Разрешённая мощность квартиры по ТУ в брифе не указана.	Без ответа: щит и группы рассчитаны на 10 кВт; при меньших ТУ — пересчёт групп варочной панели и духового шкафа.	до сборки щита
К-9	Вентканалы в брифе не показаны: принято два канала — ВК-1 в санузле у стояков (стена А) и ВК-2 у стены В бывшей кухни.	Без ответа: вытяжка кухни — рециркуляционная; вентилятор санузла — по месту ВК-1 после обмера.	до потолков
К-10	Климатический подрайон (СП 131.13330) не задан: принят не северный — жилые комнаты и кухня под потолком от 2,5 м (СП 54, п. 5.12).	Без ответа: отметки потолков жилых — по 2,5 м; при северном подрайоне уровни ниже 2,7 м пересчитать до заказа каркаса.	до заказа каркаса потолков

Полный текст каждого вопроса, варианты и рекомендация — на листах 68, 69 реестра открытых вопросов.

	Лист	№ док.	Подпись	Дата	Проект: Квартира 56 м²			
Дизайнер	Кырлан А.С.			13.11.26	Ваш проект на одной странице	Стадия	Лист	Листов
Проверил						П	3	92
Н. контр.								
Утв.								



	Лист	№ док.	Подпись	Дата	Проект: Квартира 56 м²			
Дизайнер	Кырлан А.С.			13.11.26	Визуализация: Гостиная-кухня	Стадия	Лист	Листов
Проверил						П	4	92
Н. контр.								
Утв.								

выпуск 13.11.2026 № 568a382a0d · стр. 4 из 92




	Лист	№ док.	Подпись	Дата	Проект: Квартира 56 м²			
Дизайнер	Кырлан А.С.			13.11.26				
Проверил					Визуализация спальни	Стадия	Лист	Листов
Н. контр.						П	5	92
Утв.								



	Лист	№ док.	Подпись	Дата	Проект: Квартира 56 м²			
Дизайнер	Кырлан А.С.			13.11.26				
Проверил					Визуализация детской	Стадия	Лист	Листов
Н. контр.								
Утв.						П	6	92

выпуск 13.11.2026 № 568a382a0d · стр. 6 из 92

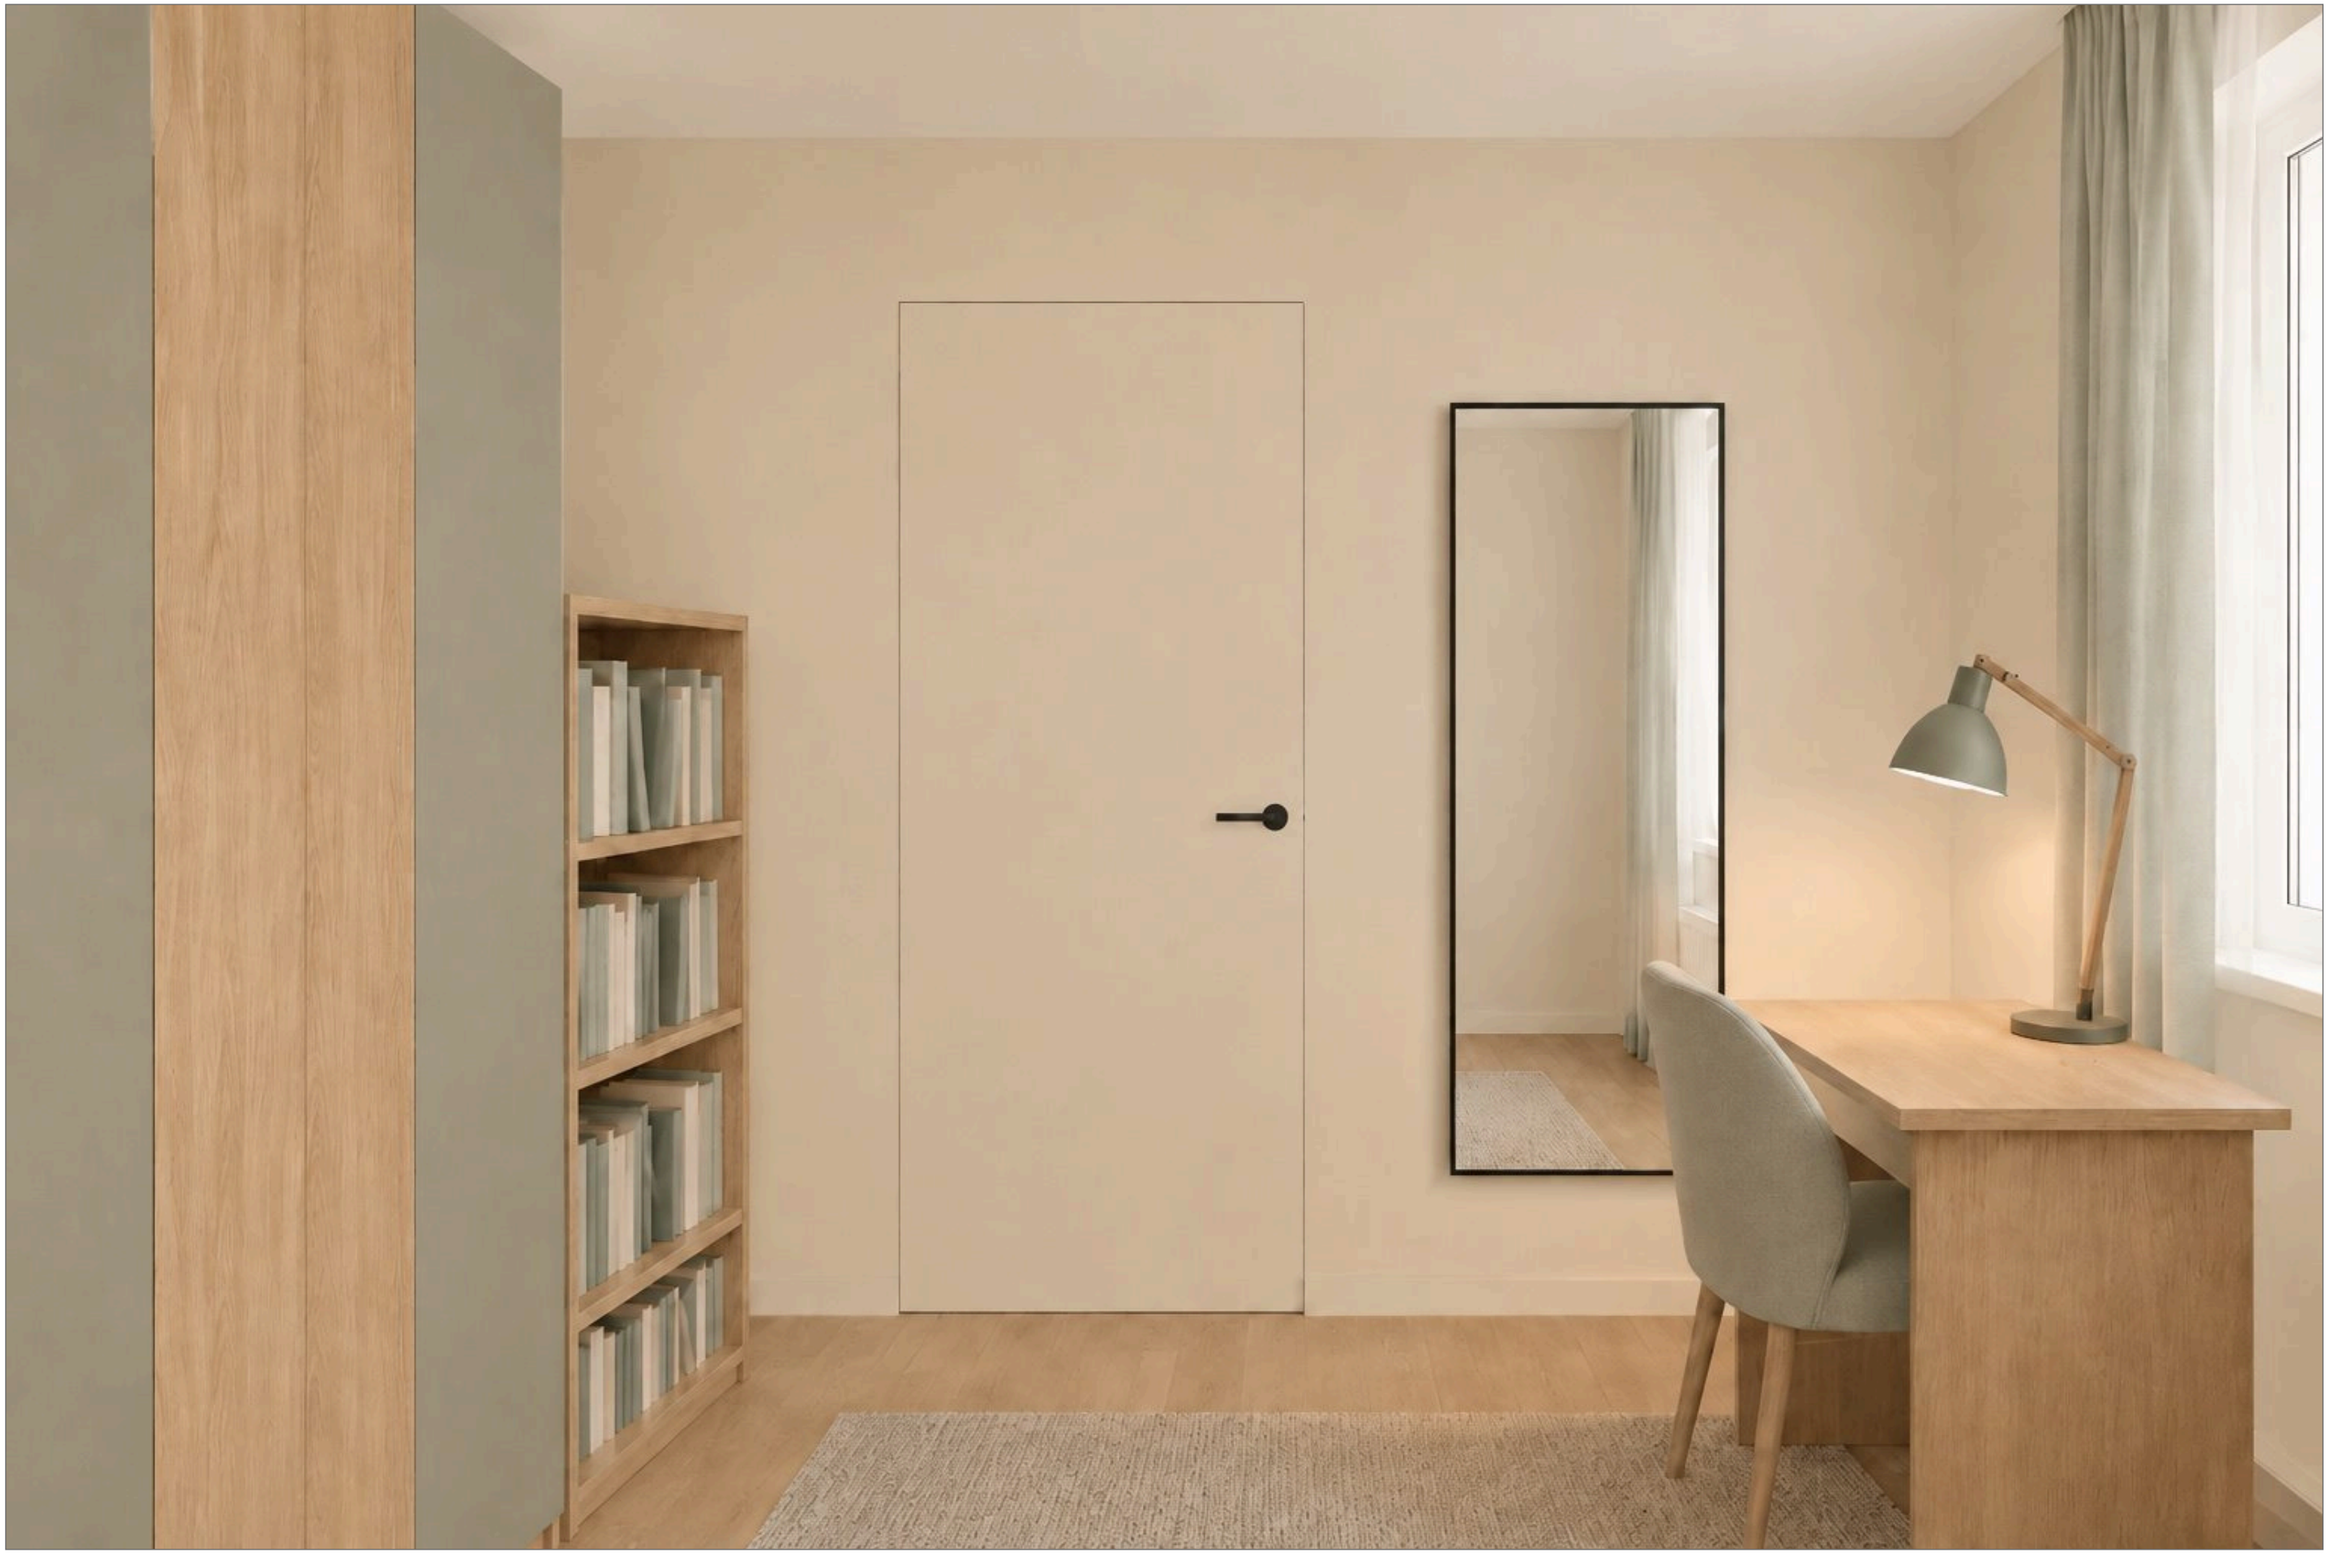

	Лист	№ док.	Подпись	Дата	Проект: Квартира 56 м²			
Дизайнер	Кырлан А.С.			13.11.26	Визуализация детской	Стадия	Лист	Листов
Проверил						П	7	92
Н. контр.								
Утв.								



	Лист	№ док.	Подпись	Дата
Дизайнер	Кырлан А.С.			13.11.26
Проверил				
Н. контр.				
Утв.				

Проект: Квартира 56 м²

Визуализация санузла	Стадия	Лист	Листов
	П	8	92

выпуск 13.11.2026 № 568a382a0d · стр. 8 из 92



	Лист	№ док.	Подпись	Дата	Проект: Квартира 56 м²			
Дизайнер	Кырлан А.С.			13.11.26				
Проверил					Визуализация санузла	Стадия	Лист	Листов
Н. контр.								
Утв.						П	9	92

Список листов

Лист	Наименование
1	Титульный лист
2	Визуализация. Вид сверху
3	Ваш проект на одной странице
4	Визуализация: Гостиная-кухня
5	Визуализация спальни
6	Визуализация детской
7	Визуализация детской
8	Визуализация санузла
9	Визуализация санузла
10	Список листов
11	Как читать альбом
12	План планировки от заказчика
13	План демонтажа и монтажа перегородок
14	План монтажный
15	Схема каркаса перегородки П-2
16	Кухня (пом. 1). Монтажная схема
17	Шкафы. Монтажная схема
18	Карта покрытий стен
19	Колерная карта
20	План размещения мебели и оборудования
21	Спецификация мебели и оборудования
22	Спецификация мебели и оборудования (продолжение)
23	Спецификация мебели и оборудования (продолжение)
24	Ведомости изделий, техники и фурнитуры
25	План выводов сантехники
26	Схема разводки водопровода и канализации
27	Аксонометрическая схема В1 (холодное водоснабжение)
28	Аксонометрическая схема Т3 (горячее водоснабжение)
29	Аксонометрическая схема К1 (канализация)
30	Развёртки мокрых зон: выводы ВК. Гостиная-кухня
31	Развёртки мокрых зон: выводы ВК. Санузел
32	Спецификация сантехнического оборудования
33	Раскладка плитки. Санузел. Развёртки стен
34	План размещения дверей
35	Ведомость заполнения проёмов
36	План потолков
37	Разрезы и узлы потолков
38	Разрезы и узлы потолков (продолжение)
39	Сечения потолков М 1:10
40	Однолинейная схема щита
41	Таблица нагрузок щита
42	План принципиальных трасс
43	План розеток и электровыводов
44	План слаботочных сетей
45	План освещения
46	Техническое задание на подбор светильников
47	Управление светильниками
48	План вентиляции
49	Ведомость воздухообмена
50	План отопления
51	План покрытий пола
52	Раскладка плитки. Планы полов
53	Раскладка плитки. Прихожая. Фартук кухни
54	Развёртка стены Г. Гостиная-кухня (пом. 1), кухонный фронт
55	Развёртка стены А. Гостиная-кухня (пом. 1)
56	Развёртка стены Б. Гостиная-кухня (пом. 1)
57	Развёртка стены В. Гостиная-кухня (пом. 1)
58	Развёртка стены А. Спальня (пом. 2)
59	Развёртка стены Б. Спальня (пом. 2)
60	Развёртка стены В. Спальня (пом. 2)
61	Развёртка стены Г. Спальня (пом. 2)
62	Развёртки стен А, Б. Детская (пом. 3)
63	Развёртки стен В, Г. Детская (пом. 3)
64	Развёртки стен А, Б. Санузел (пом. 4)
65	Развёртки стен В, Г. Санузел (пом. 4)
66	Развёртки стен А, Б. Прихожая (пом. 5)
67	Развёртки стен В, Г. Прихожая (пом. 5)
68	Открытые вопросы, принятые допущения и конфликты. Лист 1 из 2
69	Открытые вопросы, принятые допущения и конфликты. Лист 2 из 2
Д1	Шкаф распашной М-19
Д2	Шкаф распашной М-23
Д3	Шкаф-купе М-27
Д4	Система хранения М-29
Д5	Кухня (пом. 1). Развёртка гарнитура
С1	Ведомость отделки помещений
С2	Спецификация отделочных материалов
С3	Список покупок
С4	Список покупок (окончание)
С5	Смета проекта: этапы, помещения, итог
С6	Смета проекта: этапы, помещения, итог (продолжение)
С7	Смета проекта: этапы, помещения, итог (окончание)
С8	Смета материалов с ценами
С9	Смета материалов с ценами (продолжение)
С10	Смета материалов с ценами (продолжение)
С11	Смета материалов с ценами (окончание)
С12	Узлы. Лист 1 из 2
С13	Узлы. Лист 2 из 2
С14	Календарный график работ и закупок
С15	Чек-лист приёмки по этапам. Лист 1 из 3
С16	Чек-лист приёмки по этапам. Лист 2 из 3
С17	Чек-лист приёмки по этапам. Лист 3 из 3
С18	Лист → мастер

1. Размеры даны в мм от чистовых поверхностей стен: слой штукатурки 20 мм по блоку и 5 мм шпаклёвки по ГКЛ учтён. Перед заказом встроенной мебели — контрольный обмер после штукатурки.
2. Привязки мебели — от стен и углов помещения, а не от другой мебели.
3. Розетки, выводы и выключатели под мебель — см. лист 43 «План розеток и электровыводов»; сантехприборы и выводы воды — лист 25.
4. План расстановки не является документацией для изготовления мебели: изделия — по чертежам мебельщика; покупную мебель заменять только на изделия не больше габарита из спецификации (лист 21).
5. Встроенная мебель «стена в стену» — с зазором 10 мм с каждой стороны или с компенсаторами.
6. Развёртки — вид на стену изнутри помещения, по часовой стрелке; расположение стен на схеме листа развёртки; размеры — в мм по чистовым поверхностям; отметки — в м от ±0,000; высоты Н — от чистого пола помещения до оси изделия, у декора — до центра.
7. Красная цепочка — привязки электроточек и выводов по осям от угла чистовых стен; высота Н — у знака, от чистого пола до оси; высоты мебели, проёмов и границ отделки колонкой отметок слева. У знака — короткая марка; назначение, группа щита, высота и привязка каждой точки и вывода — в «Ведомости точек и выводов» под видами (каждая точка — строка).
8. У знака электроточки: марка (Р — розетка, S — выключатель, Св — светильник, ЭВ вывод кабеля), ×N — число постов в рамке, гр. — группа щита, Н — высота оси от чистого пола, мм; группы по клавишам выключателя — на листе выключателей.
9. Схема мебели, приборов и декора не является технической документацией для производства мебели; габариты — по паспортам изделий.
10. Марки позиций: М-NN — мебель, ОБ-NN — оборудование, С-NN — сантехника; О-N отделка (ведомость отделочных материалов, серия С).
11. Размеры мебели и изделий на заказ уточнить по месту после отделочных работ.

	Лист	№ док.	Подпись	Дата
Дизайнер	Кырлан А.С.			13.11.26
Проверил				
Н. контр.				
Утв.				

Проект: Квартира 56 м²

Список листов	Стадия	Лист	Листов
	П	10	92

Общие указания

выпуск 13.11.2026 № 568a382a0d · стр. 10 из 92

Что в альбоме

Альбом — дизайн-проект с рабочими чертежами для ремонта. Листы идут в порядке работ: титул и вводные, реестр открытых вопросов и решений, планы (обмер, монтаж стен, мебель, двери, потолки, полы), инженерия (сантехника, электрика, вентиляция и отопление), развёртки стен с визуализациями помещений, чертежи мебели, ведомости материалов и узлы.

Вам как заказчику — титул, эта вводная, «Ваш проект на одной странице», реестр вопросов, план мебели, визуализации и развёртки, ведомости мебели и материалов. Подрядчику — всё остальное: монтажные планы, привязки выводов и розеток, узлы, ведомости объёмов.

Знаки на листах

Без знака — решение утверждено или подтверждено обмером.

Что проверить до ремонта

1. Розетки у кровати и рабочего места: хватает ли их с каждой стороны кровати и над столом (план розеток — лист 43).

2. Выводы под технику — варочная панель, духовка, посудомойка, стиральная машина, бойлер: совпадают ли с выбранными моделями (листы 21, 22, 23, 43).

3. Высоты розеток, выключателей и выводов даны от чистого пола: если мебель или техника будут другими — скажите до штробления стен.

Номера записей

К-N — открытый вопрос: чего не хватает или что выбрать (варианты и рекомендация — в тексте). Пока ответа нет, действует строка «если решения нет».

Кф-N — конфликт между разделами (например, мебель и радиатор в одном месте); закрывается решением, которое записывается как ИЗ-N.

ИЗ-N — изменение проекта: что было, что стало и кто утвердил. Изменение без подписи предложение.

Все записи — на листе реестра сразу после вводных; на других листах на них стоят ссылки.

Почему альбом предварительный

Обмера на объекте не было: размеры взяты с плана заказчика. Технические условия (мощность, вода, вентиляция дома) не получены, часть решений ждёт вашего ответа. Пока в реестре есть открытые вопросы, альбом предварительный — пометка в штампе снимается закрытием вопросов, а не стиранием.


Правку к любому листу можно оставить по кнопке «Правка к листу» или на сайте студии: дизайн-студия-квартир.рф — укажите номер листа и что изменить.

3 круга правок входят в цену; условия — в договоре и на странице вашего заказа на сайте студии.

Шифр проекта ГД-2026-011-АИ

	Лист	№ док.	Подпись	Дата	Проект: Квартира 56 м²			
Дизайнер	Кырлан А.С.			13.11.26	Как читать альбом	Стадия	Лист	Листов
Проверил						П	11	92
Н. контр.								
Утв.								

выпуск 13.11.2026 № 568a382a0d · стр. 11 из 92

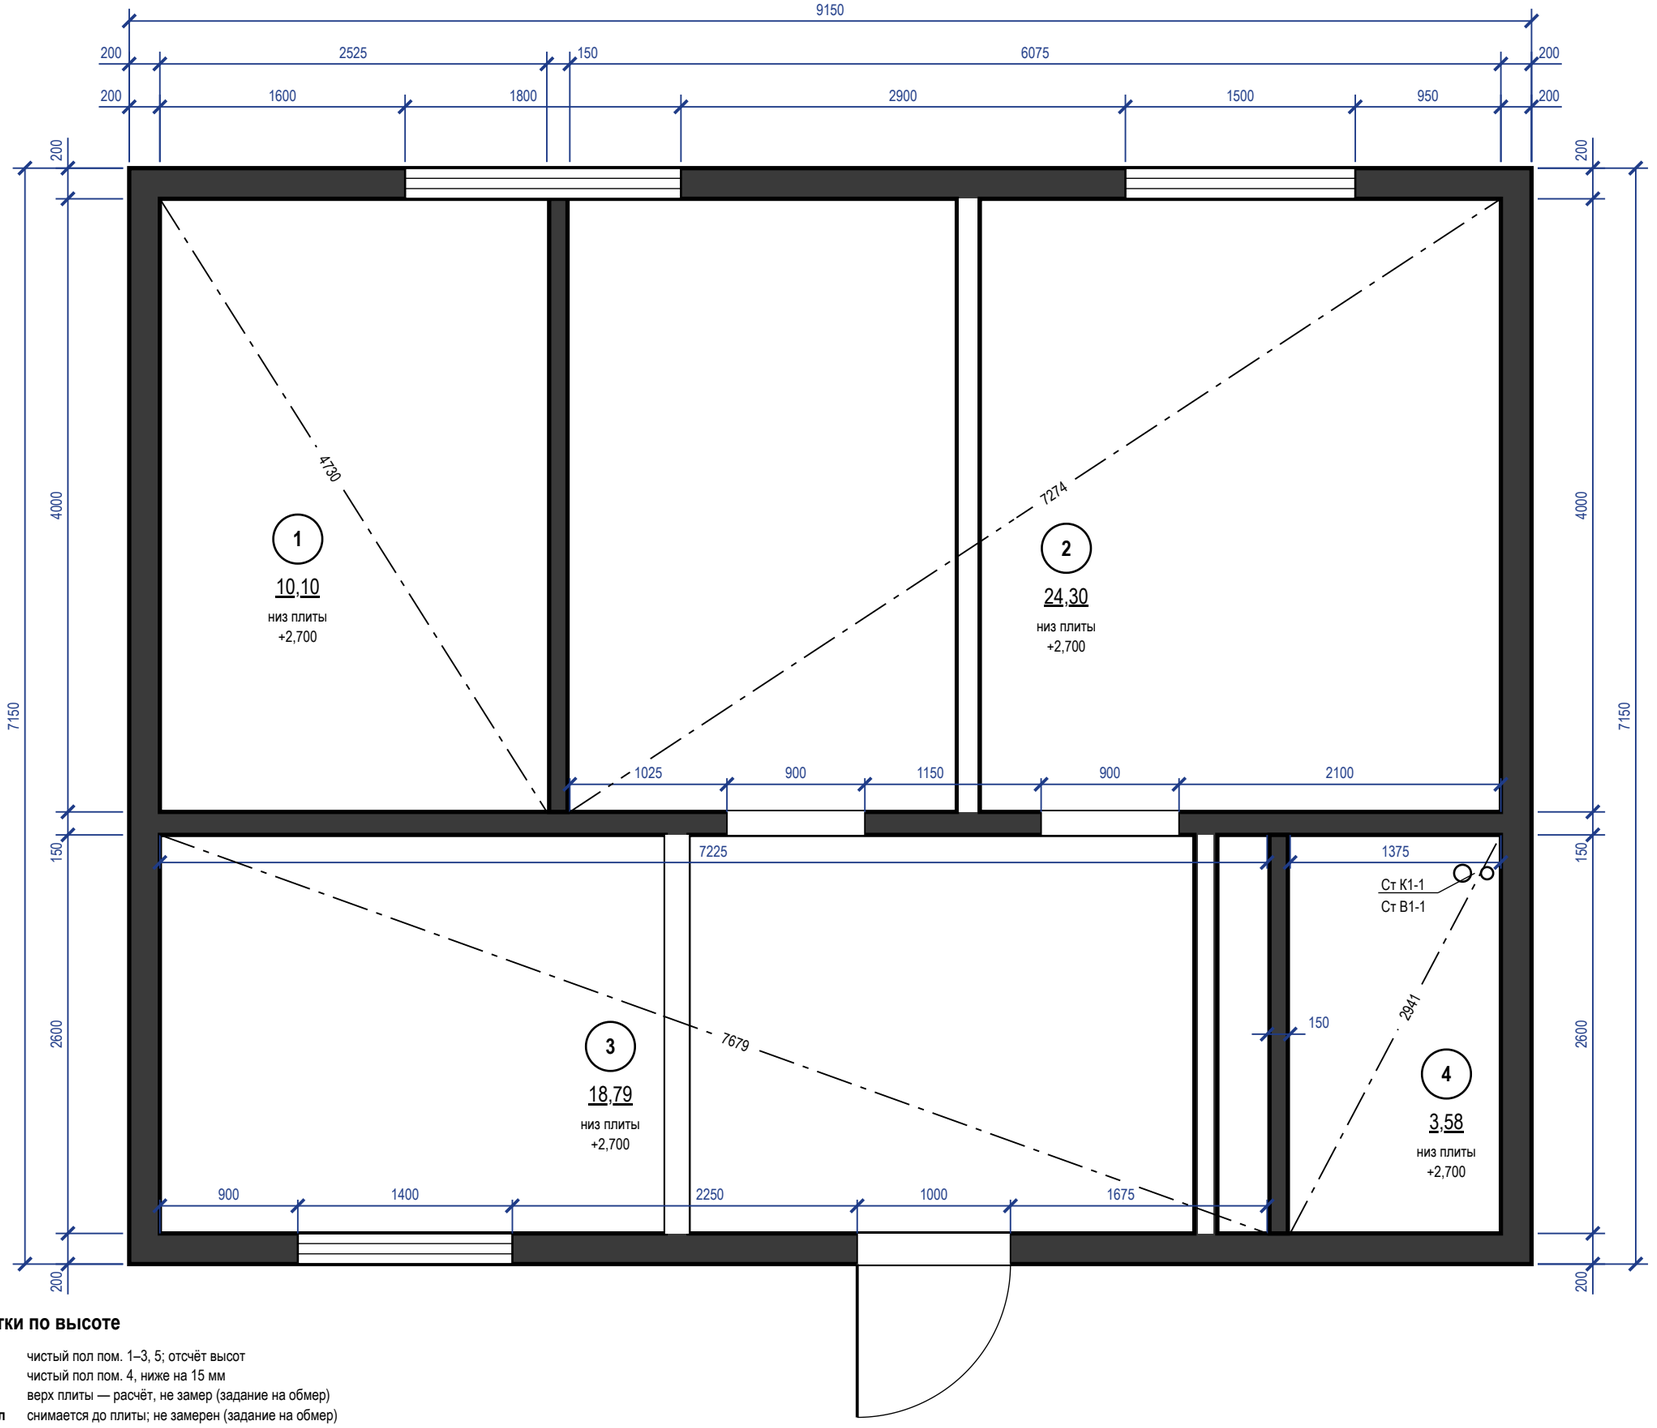

Экспликация помещений

№	Наименование	Площадь, м²
1	Кухня	10,10
2	Гостиная	24,30
3	Прихожая	18,79
4	Санузел	3,58
	Итого (общая площадь)	**56,77**

Условные обозначения

- существующие стены (сечение)
- окно (рама, остекление)
- проём существующий, без заполнения (откосы)
- стояк: К1 — канализация, В1 — ХВС, Т3 — ГВС
- диагональ помещения — контроль прямоугольности
- (1) номер помещения, площадь м²

Примечания

1. Размеры — в мм по чистым поверхностям стен до отделки (по плану заказчика); площади — в м² по тем же размерам. До начала работ выполнить контрольный обмер.
2. За отметку ±0,000 принят чистый пол, не существующий (блок отметок). «Низ плиты» у марки помещения — отметка низа плиты перекрытия от ±0,000, как на развёртках и плане потолков (не высота потолка: потолок — по плану потолков).
3. Толщины стен: наружные 200 мм, перегородки 150 мм; отличающиеся толщины и уступы — размерами на плане.
4. Обмер — существующее положение: С-1, С-2 показаны как существующие, их снос — на плане демонтажа; новых конструкций на обмере нет.
5. Помещения и экспликация — до перепланировки (границы и назначение приняты по данным заказчика, не обмерены). Общая площадь до перепланировки 56,77 м², после — 56,37 м² (экспликация «после» лист 13); разница −0,40 м² — площадь сносимых и новых перегородок.
6. Несущие стены не определены: до технического заключения все стены считать несущими; проёмы и штробы в них не выполнять.
7. Дверные проёмы показаны без заполнения (двери — лист 35); высота дверных проёмов 2100 мм; низ окон (подоконник) 850, 900 мм от чистого пола, высота окон 1500, 1450 мм.
8. Диагонали — контрольные размеры; расхождение более 5 мм подписать на плане как перекос.
9. Размеры проверить на месте до начала работ; расхождение контрольных промеров ≤ 2 %.

Отметки по высоте

±0,000	чистый пол пом. 1–3, 5; отсчёт высот
−0,015	чистый пол пом. 4, ниже на 15 мм
−0,064	верх плиты — расчёт, не замер (задание на обмер)
сущ. пол	снимается до плиты; не замерен (задание на обмер)


	Лист	№ док.	Подпись	Дата
Дизайнер	Кырлан А.С.			13.11.26
Проверил				
Н. контр.				
Утв.				

Проект: Квартира 56 м² — **М 1:40**

План планировки от заказчика

Стадия	Лист	Листов
П	12	92

выпуск 13.11.2026 № 568a382a0d · стр. 12 из 92

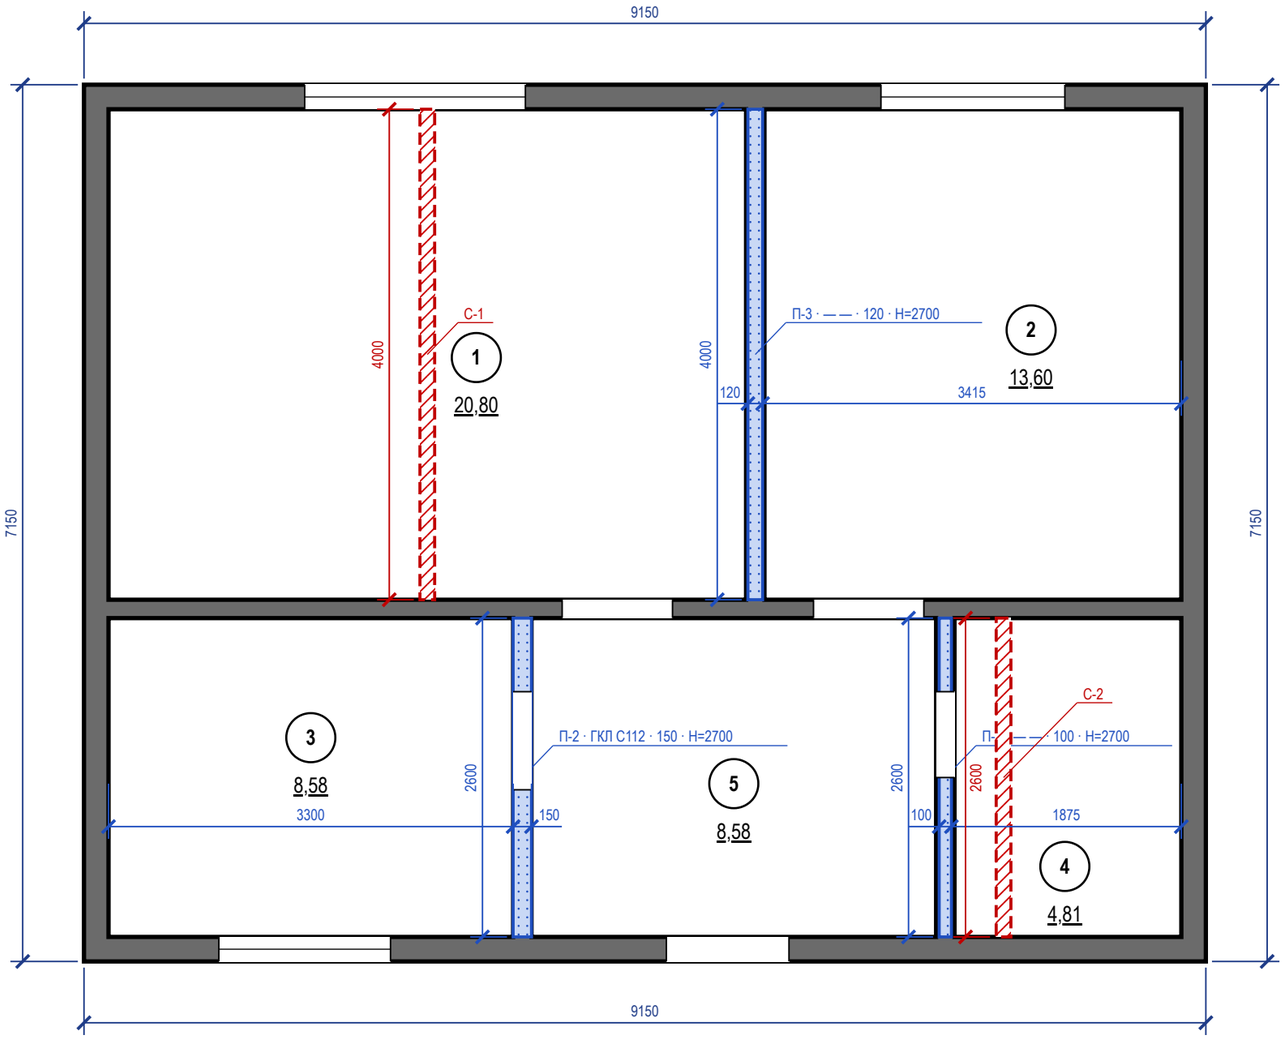


Ведомость демонтажа и монтажа

Марка	Конструкция	Длина, мм	Толщ., мм	Высота	Примечание
С-1	демонтаж: перегородка	4000	120	2700	перегородка кухня/гостиная, объединение в кухню-гостиную
С-2	демонтаж: перегородка	2600	120	2700	старая стена санузла, расширение мокрой зоны
П-1	монтаж: Пеноблок D500, армирование через 2 ряда, штукатурка с двух сторон,	2600	100	H=2700	новая стена санузла, пеноблок под гидроизоляцию
П-2	монтаж: ГКЛ 12,5 мм в 2 слоя с каждой стороны по металлическому каркасу ПС/ПН, минеральная вата 50 мм, С112	2600	150	H=2700	перегородка детская/прихожая, ГКЛ со звукоизоляцией
П-3	монтаж: Кирпич керамический полнотелый, кладка в полкирпича, штукатурка с двух сторон,	4000	120	H=2700	перегородка спальня/гостиная, кирпич для звукоизоляции

Условные обозначения

- существующие стены — сохраняются; несущие не определены — считать несущими
- демонтируемые конструкции (красным)
- новое — возводится по проекту (синим)
- проём существующий, без заполнения (откосы)
- (1) номер помещения, площадь м²

Отметки по высоте

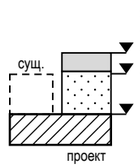


±0,000	чистый пол пом. 1–3, 5; отсчёт высот
−0,015	чистый пол пом. 4, ниже на 15 мм
−0,064	верх плиты — расчёт, не замер (задание на обмер)
сущ. пол	снимается до плиты; не замерен (задание на обмер)

Примечания

1. Демонтаж несущих стен и плит перекрытия не производится; снос несущих конструкций — только по техническому заключению (в ведомости).
2. Новые перегородки и фальш-стены (синим) привязаны от капитальных стен и наружного контура; высота — по ведомости («до плиты» — до низа плиты перекрытия); проёмы в них усилить стойками каркаса.
3. Перепланировку согласовать до начала работ (ЖК РФ, ст. 26); план не передавать в работу до допуска главного инженера проекта.
4. Дверные блоки — по плану дверей (лист 34); существующие проёмы не расширяются.
5. Демонтаж существующих покрытий пола, стен и потолка, дверных блоков и сантехприборов (если есть) — до основания; объёмы демонтажа — для справки, по факту на объекте.
6. За отметку ±0,000 принят чистый пол, не существующий (блок отметок). Размеры — в мм по чистовой поверхности стен до отделки.
7. Размеры проверить на месте до начала работ: расхождение с обмером — не более 2 % (иначе — к архитектору).
8. Несущие стены не определены: до технического заключения все стены считать несущими — проёмы, ниши и штробы в них не выполнять.

	Лист	№ док.	Подпись	Дата	Проект: Квартира 56 м²			М 1:50
Дизайнер	Кырлан А.С.			13.11.26	План демонтажа и монтажа перегородок	Стадия	Лист	Листов
Проверил						П	13	92
Н. контр.								
Утв.								

выпуск 13.11.2026 № 568a382a0d · стр. 13 из 92

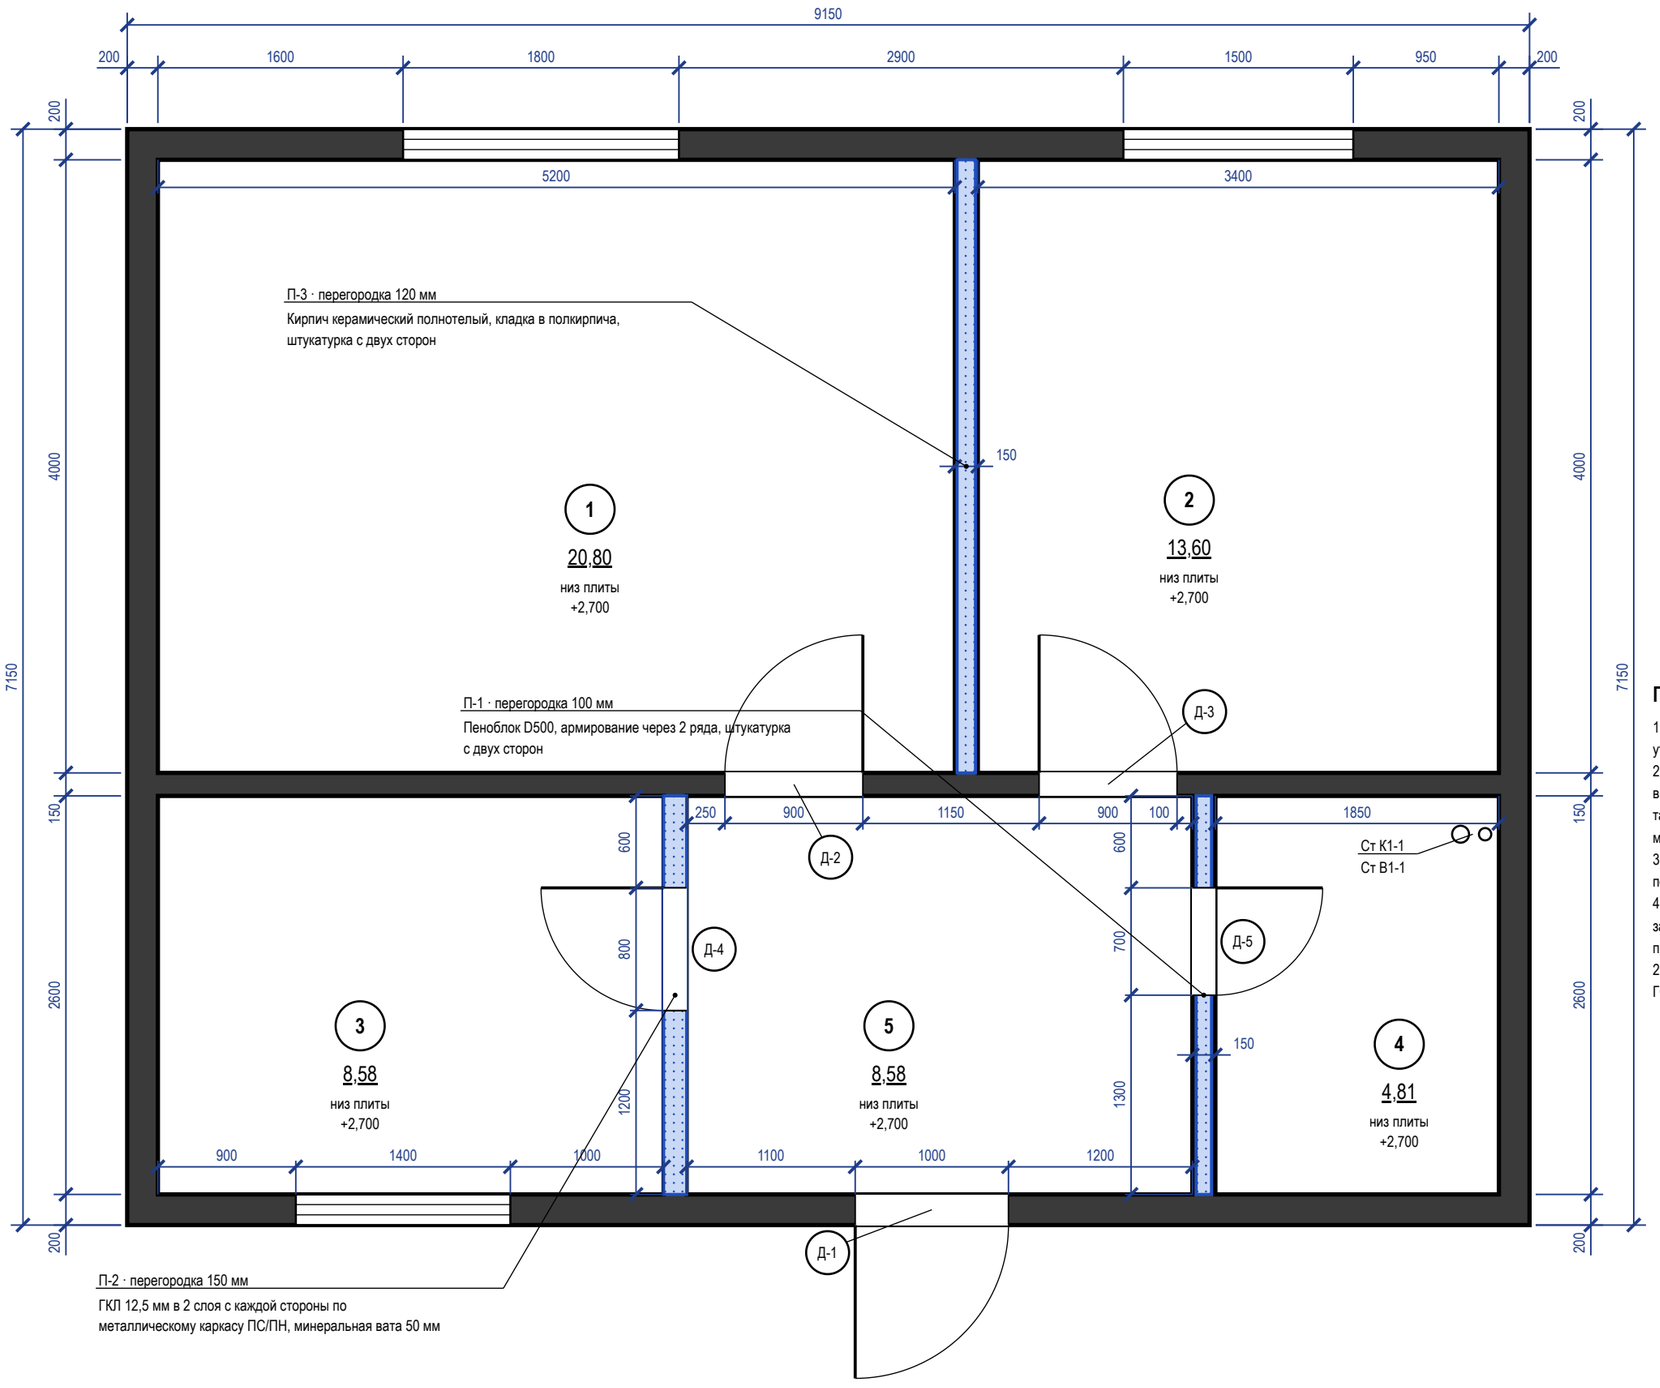

Экспликация помещений

№	Наименование	Площадь, м²
1	Гостиная-кухня	20,80
2	Спальня	13,60
3	Детская	8,58
4	Санузел	4,81
5	Прихожая	8,58
	Итого (общая площадь)	**56,37**

Таблица проёмов

Марка	Наименование	Проём ш×в, мм	Полотно (расч.)
Д-1	Дверь входная	1000×2100	блок — задать
Д-2	Дверь скрытого монтажа	900×2100	800×2000
Д-3	Дверь скрытого монтажа	900×2100	800×2000
Д-4	Дверь скрытого монтажа	800×2100	700×2000
Д-5	Дверь скрытого монтажа	700×2100	600×2000

Примечания

1. Размеры — в мм от чистовых поверхностей стен до отделки; размеры уточнить по месту до начала работ.
2. Новые перегородки и облицовки — синим; каркас и обшивка — по выноскам. Д-N, ПР-N в кружке — марка проёма: проём и полотно — по таблице проёмов, «расч.» — полотно по проёму, заказ — по выбранной модели; ведомость, отделка и фурнитура — лист 35.
3. Несущие стены не изменять: проёмы, ниши и штробы в них — только по техническому заключению.
4. «расч.» — полотно, выведенное из проёма по запасу каталогов; заказ — по таблице проёмов выбранной модели; Д-2, Д-3, Д-4, Д-5: проём 2100, а под полотно 2000 по каталогам нужен 2050–2080, под 2100 — 2150–2180: высоту проёма — по модели; Д-1: входной блок по ГОСТ 31173-2016 — задать при выборе блока.

	Лист	№ док.	Подпись	Дата
Дизайнер	Кырлан А.С.			13.11.26
Проверил				
Н. контр.				
Утв.				


Проект: Квартира 56 м² — **М 1:40**

План монтажный

Стадия	Лист	Листов
П	14	92

выпуск 13.11.2026 № 568a382a0d · стр. 14 из 92


Вид на каркас без обшивки (М 1:25)

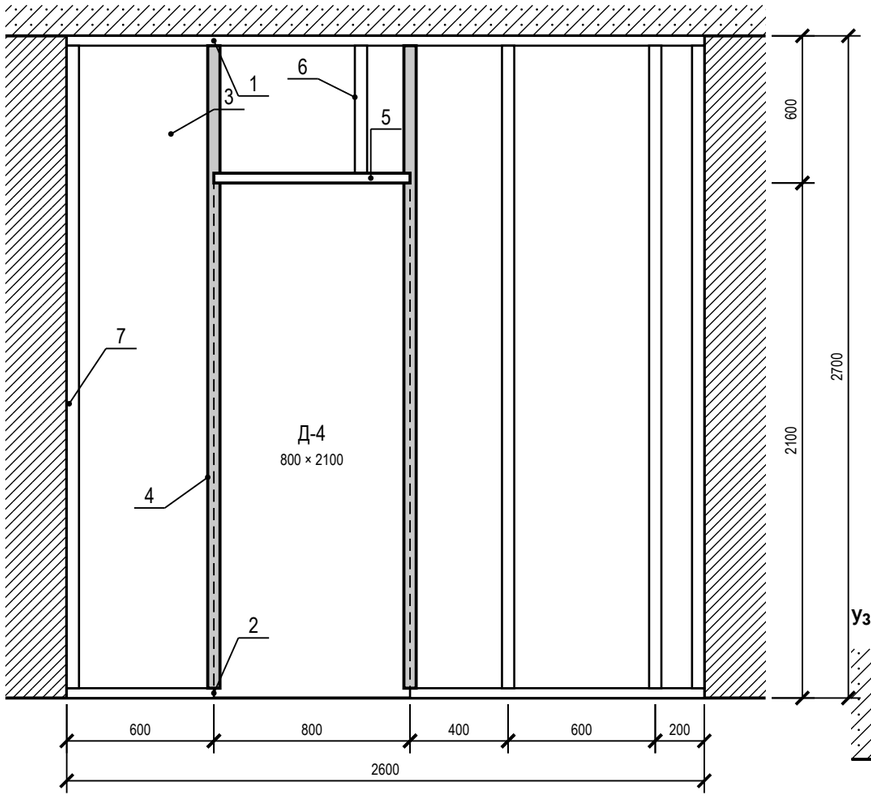

Оси — стойки каркаса; полки профиля на виде условны

Сечение А–А по стойке (М 1:5)


сверху — пом. 3, окраска

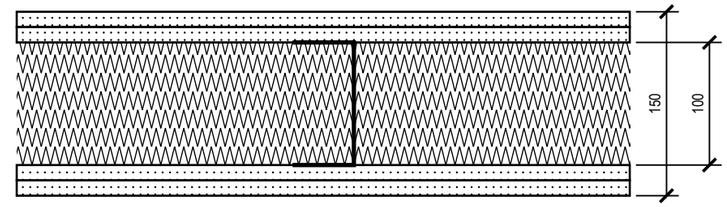

снизу — пом. 5, окраска

поз. 9 — ГКЛ 12,5 мм в 2 слоя с каждой стороны; поз. 3 — ПС 100; поз. 8 — минвата 100 мм (принято)

Сечение Б–Б у проёма, на уровне ниже перемычки (М 1:5)

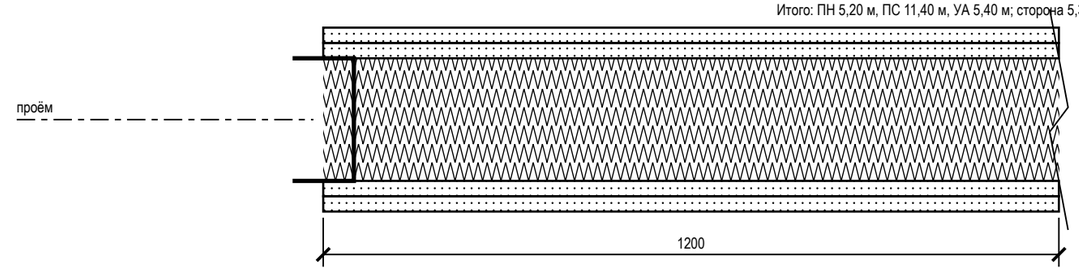


поз. 4 — УА 100, обрамление проёма; обшивка по краю проёма, простенок 1200 мм до пилона (на сечении показан с обрывом)

Ведомость элементов каркаса


Поз.	Наименование	Кол-во	Ед.
1	ПН 100 по потолку (к перекрытию)	2,60	м
2	ПН 100 по полу, без проёма	1,80	м
3	ПС 100 через 600 мм	4 × 2,70	м
4	УА 100 по краям проёма	2 × 2,70	м
5	ПН 100 перемычка над проёмом	0,80	м
6	ПС 100 над перемычкой	1 × 0,60	м
7	Лента уплотнительная под профили	9,80	м
8	Минвата в полость, 100 мм	5,34	м²
9	ГКЛ 12,5 мм, 2 слоя с двух сторон	21,36	м²

Итого: ПН 5,20 м, ПС 11,40 м, УА 5,40 м; сторона 5,34 м²

Узел 1. К плите (М 1:5)

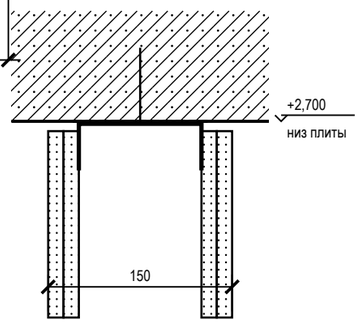

Узел 2. К полу (М 1:5)

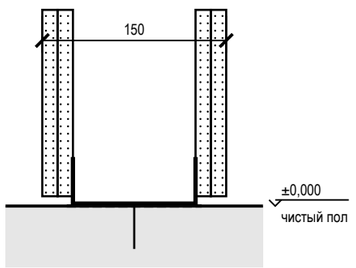

Примечания

1. П-2 (С112, ГКЛ в 2 слоя с каждой стороны, толщина 150 мм, высота 2700 мм до плиты); ось и длина 2600 мм — со скана плана заказчика (контрольный обмер не выполнялся).
2. Шаг стоек 600 мм — по данным (под плитку и во влажной зоне). Размеры сечений профилей — «ПС 100», «УА 100» по данным и каталогу; толщины листов — ГОСТ 32614-2012.
3. Шаг стоек 600 мм принят по базовому правилу: в проекте шаг не задан.
4. Проём Д-4 в каркасе 800 × 2100 мм принят по размеру полотна: короб скрытой двери (модель, размеры) не выбран — проём пересчитать по коробке до монтажа УА.
5. Перемычка над проёмом — направляющий профиль по верху проёма на всю его ширину; короткие стойки ПС над перемычкой на шаге каркаса: по практике узла Knauf, не по данным объекта.
6. Заполнение полости — минераловатная плита на всю глубину профиля (Rw системы С112 нормируют с заполнением); марка и плотность выбираются при закупке.
7. Длина стойки равна высоте перегородки: стойки режут на высоту между направляющими при монтаже, зазоры до плиты и пола в проекте не заданы.
8. Обшивку крепят к стойкам шурупами через слой, швы слоёв вразбежку; зазоры обшивки до плиты и пола, шаг дюбелей, марка заполнения — по ТУ системы и узлу изготовителя.

	Лист	№ док.	Подпись	Дата
Дизайнер	Кырлан А.С.			13.11.26
Проверил				
Н. контр.				
Утв.				


Проект: Квартира 56 м² — **по видам**

Схема каркаса перегородки П-2


Стадия	Лист	Листов
П	15	92

выпуск 13.11.2026 № 568a382a0d · стр. 15 из 92

Привязка выводов и крепление модулей (М 1:25)

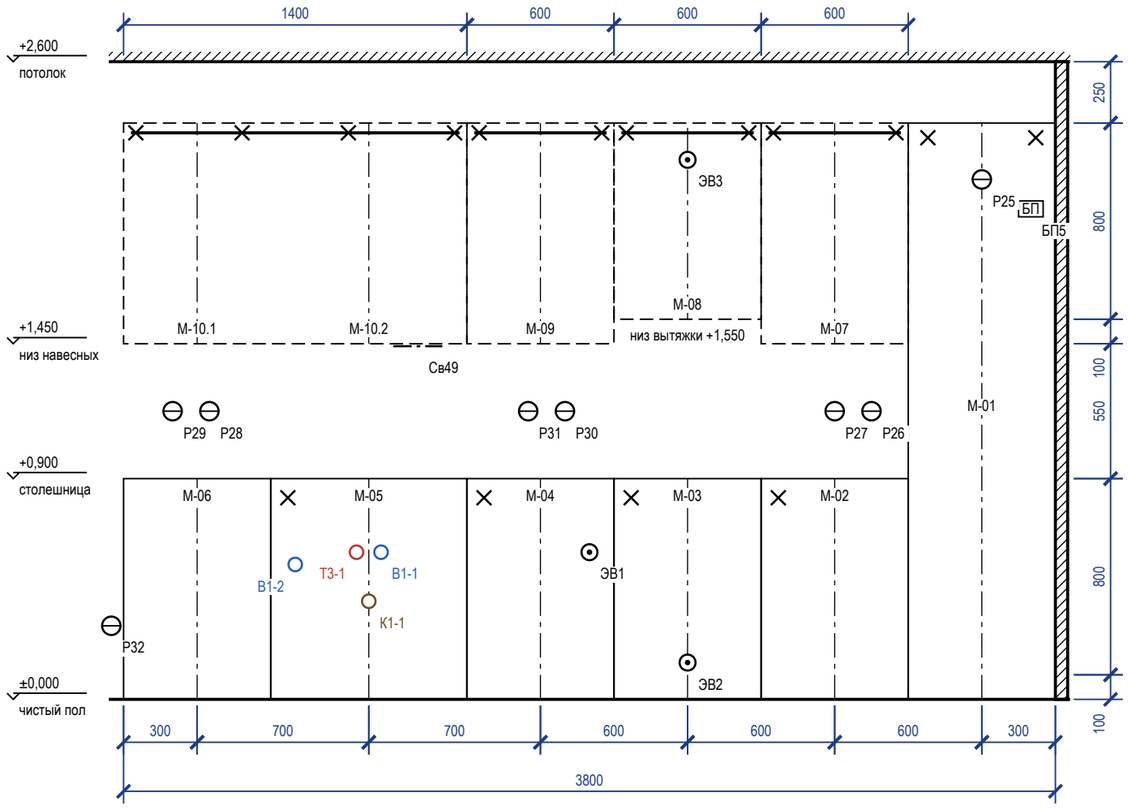

План столешницы (М 1:25)

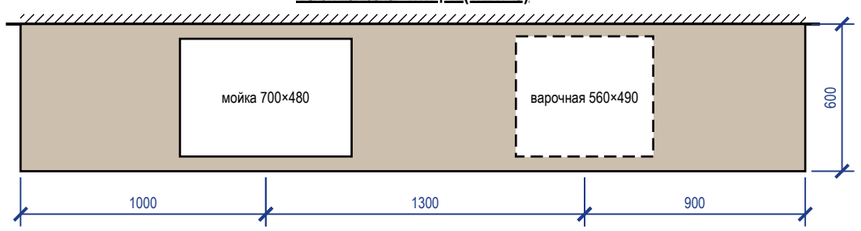

Примечания

1. Выводы — по проекту электрики и ВК; привязка по горизонтали — от оси модуля (плюс — вправо по виду), по высоте — от чистого пола до оси вывода.
2. Пенал — уголки к стене 2 шт. сверху; нижние модули — стяжками между собой и уголком к стене; ряд выставить по уровню опорами цоколя.
3. Розетки над столешницей — не ниже 150 мм над ней и не за корпусом техники; розетка за ПММ, духовым шкафом и холодильником — только в соседнем модуле или в зоне цоколя с доступом.
4. Столешница — вырезы по шаблонам выбранных моделей мойки и варочной панели; торцы у стены — герметик, пристеночный плинтус.

Привязка выводов к осям модулей

Код	Назначение	Модуль	От оси, мм	Н, мм	Размещение
Р32	розетка — посудомоечная машина (на стене за торцом гарнитура, доступ сбоку)			300	вне гарнитура
Р29	розетка — фартук	М-06	−100	1175	над столешницей (фартук)
Р28	розетка ×2 — фартук	М-06	+50	1175	над столешницей (фартук)
В1-2	В1 — кран ПММ в шкафу мойки	М-05	−300	550	в модуле мойки
Т3-1	Т3 — межос. 100	М-05	−50	600	в модуле мойки
К1-1	К1 Ø50 — мойка	М-05	0	400	в модуле мойки
В1-1	В1 — межос. 100	М-05	+50	600	в модуле мойки
Св49	светодиодная лента — подсветка столешницы	М-05	+200	1440	в профиле по низу навесного модуля
Р31	розетка — фартук между мойкой и варочной	М-04	−50	1175	над столешницей (фартук)
Р30	розетка ×2 — фартук между мойкой и варочной	М-04	+100	1175	над столешницей (фартук)
ЭВ1	вывод кабеля — варочная панель — в соседнем модуле, за ящиком	М-04	+200	600	в соседнем модуле, за ящиком
ЭВ2	вывод кабеля — духовой шкаф	М-03	0	150	под духовым шкафом, доступ через ящик
ЭВ3	вывод кабеля — вытяжка — над корпусом	М-08	0	2200	в навесном модуле
Р27	розетка — фартук	М-02	0	1175	над столешницей (фартук)
Р26	розетка ×2 — фартук	М-02	+150	1175	над столешницей (фартук)
Р25	розетка — холодильник — над нишей, съёмная панель	М-01	0	2120	над нишей холодильника, съёмная панель
БП5	блок питания — в колонне М-01 над нишей холодильника, верх, съёмная панель	М-01	+200	2000	над нишей холодильника, съёмная панель

Зазоры под отделку

Поверхность	Отделка	Зазор, мм	Учесть
фартук	керамогранит	10	от чернового основания до корпуса навесных и столешницы
стены	окраска	5	под штукатурку и шпаклёвку за пеналом
пол	инженерная доска		цоколь — после укладки пола, опоры ±20 мм


Условные обозначения

- нижний модуль, пенал (контур)
- невидимый контур: навесной модуль, корпус под столешницей
- ось модуля (от неё — привязка вывода)
- анкер / уголок крепления к стене
- розетка на стене
- вывод кабеля к технике
- В1 — вывод воды В1 / Т3, канализации К1


	Лист	№ док.	Подпись	Дата	Проект: Квартира 56 м²		М 1:25	
Дизайнер	Кырлан А.С.			13.11.26	Кухня (пом. 1). Монтажная схема	Стадия	Лист	Листов
Проверил						П	16	92
Н. контр.								
Утв.								

выпуск 13.11.2026 № 568a382a0d · стр. 16 из 92


Шкаф распашной М-19 (пом. 2) (М 1:25)

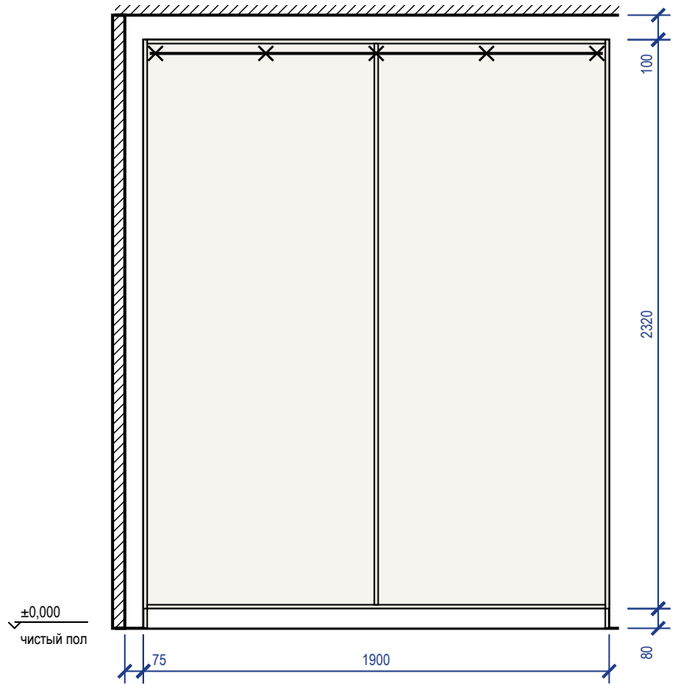


Шкаф распашной М-23 (пом. 3) (М 1:25)

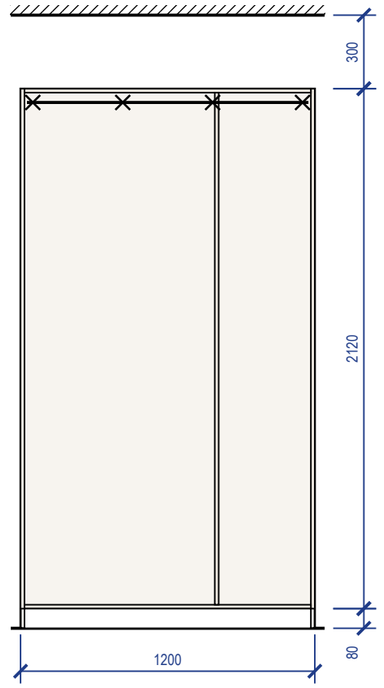

Шкаф-купе М-27 (пом. 5) (М 1:25)

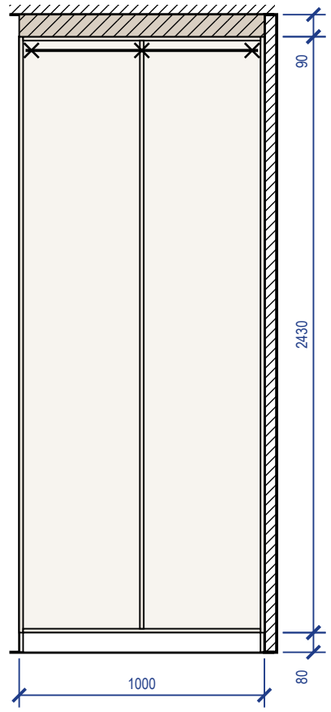

Система хранения М-29 (пом. 5) (М 1:25)

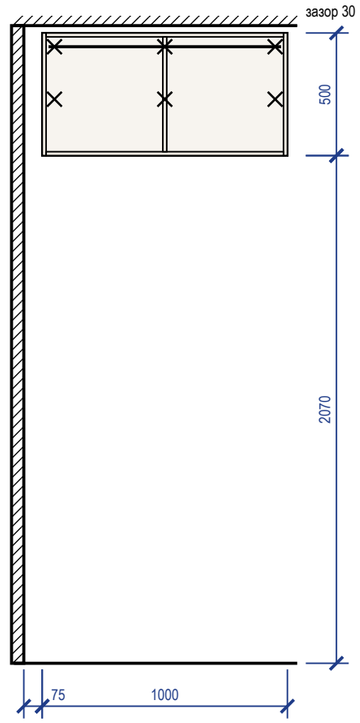

Крепление и зазоры под отделку

Марка	Помещение, стена	Основание	Отделка стены	Зазор, мм	Крепёж по планке	От опрокидывания
М-19	Спальня (2), стена В	по основанию — см. таблицу крепежа	окраска	5	анкер 5 шт., шаг 450	уголок к стене, 2 шт.
М-23	Детская (3), стена А	по основанию — см. таблицу крепежа	окраска	5	анкер 4 шт., шаг 367	уголок к стене, 2 шт.
М-27	Прихожая (5), стена В	по основанию — см. таблицу крепежа	окраска	5	анкер 3 шт., шаг 450	уголки 2 шт.
М-29	Прихожая (5), стена В	по основанию — см. таблицу крепежа	окраска	5	анкер 6 шт. (2 ряда)	уголки 2 шт.

Крепёж по основанию стены

Основание стены	Крепёж
бетон, ж/б	анкер-шуруп 7,5×72 или дюбель 8×60 с шурупом 5×70
кирпич полнотелый	дюбель 8×80 с шурупом 5×90
газобетон, пазогребень	дюбель для газобетона 10×100 или химический анкер
гипсокартон	закладная до обшивки (брус 40×80 или фанера 18 мм), саморез в закладную

Условные обозначения


- анкер / уголок крепления к стене
- корпус и полки ЛДСП (вид на стену)
- компенсатор — короб до потолка

Примечания

1. Установочные размеры — от чистого пола и чистых стен; перед установкой контрольный замер после отделки.
2. Порядок: корпус выставить по уровню опорами цоколя → закрепить к стене по задней планке → навесить двери и фасады, отрегулировать зазоры → подогнать и закрепить компенсатор.
3. Анкеры — с шагом не более 500 мм, не ближе 50 мм от края планки; на ГКЛ только в закладную, установленную до обшивки.
4. Скрытые коммуникации под анкеры проверить детектором; трассы электрики по плану розеток.

	Лист	№ док.	Подпись	Дата	Проект: Квартира 56 м²	М 1:25		
Дизайнер	Кырлан А.С.			13.11.26				
Проверил					Шкафы. Монтажная схема	Стадия	Лист	Листов
Н. контр.						П	17	92
Утв.								

выпуск 13.11.2026 № 568a382a0d · стр. 17 из 92

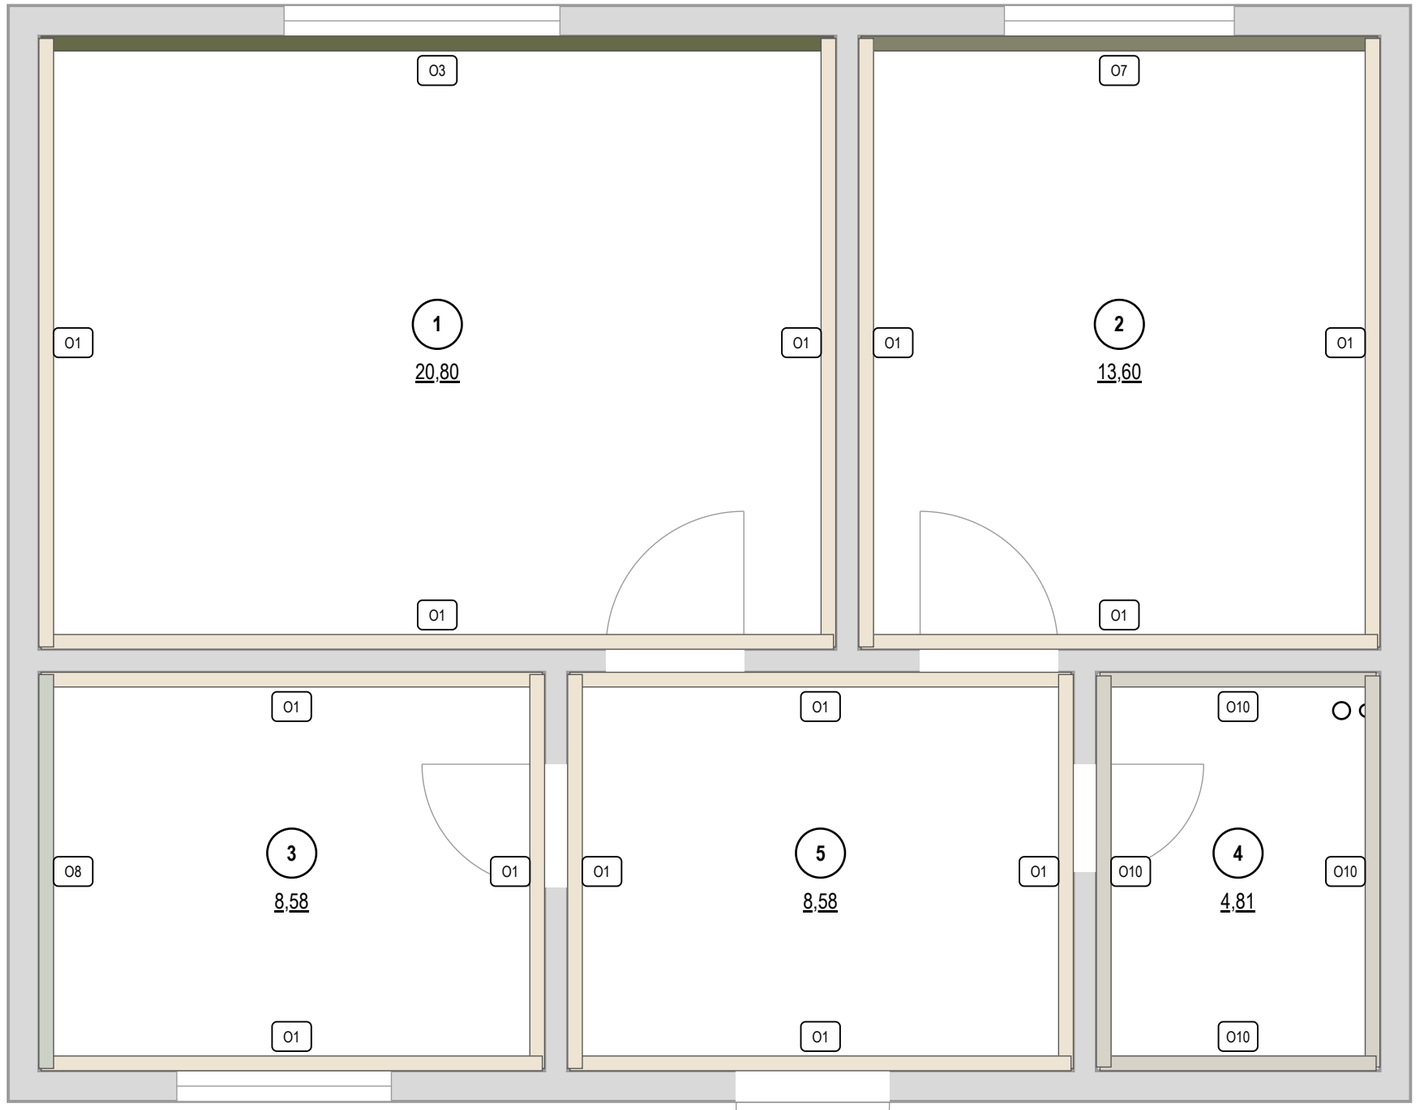

Покрытия стен

Марка	Покрытие	Помещение: S, м²	Итого, м²
O1	окраска Tikkurila · S 0804-Y30R «S 0804-Y30R»	1: 30,4; 2: 21,6; 3: 19,4; 5: 18,8	90,2
O3	окраска Farrow & Ball · No. 298 «Bancha»	1: 11,3	11,3
O7	окраска Tikkurila · S 5010-G70Y «S 5010-G70Y»	2: 6,6	6,6
O8	окраска Tikkurila · X447 «Sea Smoke»	3: 6,4	6,4
O10	облицовка плиткой Atlas Concorde · A8UZ «Marvel Travertine» 600×1200 мм	4: 19,5	19,5

Площади — нетто, по развёрткам (за вычетом проёмов и фартука); высоты помещений — от чистого пола.

	Лист	№ док.	Подпись	Дата
Дизайнер	Кырлан А.С.			13.11.26
Проверил				
Н. контр.				
Утв.				

Проект: Квартира 56 м² — **М 1:40**

Карта покрытий стен

Стадия	Лист	Листов
П	18	92

выпуск 13.11.2026 № 568a382a0d · стр. 18 из 92

Колерная карта по помещениям

Помещение	Поверхность	Образец	Поз.	Система и код цвета	Производитель, линейка / материал, артикул	Блеск	Класс истирания	LRV	Площадь
1. Гостиная-кухня 20,8 м²	стены		**K1**	NCS S 0804-Y30R	Tikkurila · Euro Power 7, колеровка по NCS	матовая	1	78	30,6 м²
	акцент А		**K2**	Farrow & Ball No. 298	Farrow & Ball · Modern Emulsion	матовая	1	≈14	10,8 м²
	потолок		**K3**	Tikkurila F485	Tikkurila · Euro Power 7	глубокомат.	2	83	20,8 м²
	пол		**KM1**	по образцу	Coswick · Классическая · арт. 1167-1101				20,8 м²
	плинтус		**K4**	NCS S 0804-Y30R	МДФ · в цвет NCS			78	17,5 м
	фартук		**KM2**	по образцу	керамогранит · аналог по хар.				1,8 м²
2. Спальня 13,6 м²	стены		**K1**	NCS S 0804-Y30R	Tikkurila · Euro Power 7, колеровка по NCS	матовая	1	78	21,9 м²
	акцент А		**K5**	NCS S 5010-G70Y	Tikkurila · Euro Power 7, колеровка по NCS	матовая	1	22	6,3 м²
	потолок		**K3**	Tikkurila F485	Tikkurila · Euro Power 7	глубокомат.	2	83	13,6 м²
	пол		**KM1**	по образцу	Coswick · Классическая · арт. 1167-1101				13,6 м²
	плинтус		**K4**	NCS S 0804-Y30R	МДФ · в цвет NCS			78	13,9 м
3. Детская 8,58 м²	стены		**K1**	NCS S 0804-Y30R	Tikkurila · Euro Power 7, колеровка по NCS	матовая	1	78	19,3 м²
	акцент Г		**K6**	Tikkurila X447	Tikkurila · Euro Power 7	матовая	1	63	6,5 м²
	потолок		**K3**	Tikkurila F485	Tikkurila · Euro Power 7	глубокомат.	2	83	8,6 м²
	пол		**KM1**	по образцу	Coswick · Классическая · арт. 1167-1101				8,6 м²
	плинтус		**K7**	NCS S 0804-Y30R	Orac Decor · Contour (Luxxus)			78	11,0 м
4. Санузел 4,81 м²	стены		**KM3**	Marvel Travertine	Atlas Concorde · арт. A8UZ				19,9 м²
	потолок		**K8**	Tikkurila F485	Tikkurila · Euro Power 7	матовая	1	83	4,8 м²
	пол		**KM4**	по образцу	керамогранит · аналог по хар.				4,8 м²
5. Прихожая 8,58 м²	стены		**K1**	NCS S 0804-Y30R	Tikkurila · Euro Power 7, колеровка по NCS	матовая	1	78	17,5 м²
	потолок		**K3**	Tikkurila F485	Tikkurila · Euro Power 7	глубокомат.	2	83	8,6 м²
	пол		**KM5**	Marvel Travertine	Atlas Concorde · арт. A8UZ				8,6 м²
	плинтус		**K4**	NCS S 0804-Y30R	МДФ · в цвет NCS			78	7,5 м

Перечень выкрасов на согласование

№	Код	Бренд / веер	Пом. / стена	Подложка	Формат	Статус
1	S 0804-Y30R	NCS Tikkurila	1, 2, 3, 5	ГКЛ с грунтом; МДФ под эмаль	600×1000; 300×600	к выполнению
2	No. 298	Farrow & Ball	1 А	ГКЛ с грунтом	600×1000	к выполнению
3	F485	Tikkurila	1, 2, 3, 4, 5	ГКЛ с грунтом	600×1000	к выполнению
4	S 5010-G70Y	NCS Tikkurila	2 А	ГКЛ с грунтом	600×1000	к выполнению
5	X447	Tikkurila	3 Г	ГКЛ с грунтом	600×1000	к выполнению

Примечания

1. Цвет на листе и на экране — ориентир. До покраски — выкрас на объекте: не меньше А3 (или лист ГКЛ), на грунте под эту краску, не на белой шпаклёвке, в 2 слоя; на обороте — код, бренд, веер, дата. Смотреть днём и вечером, рядом с образцами пола и плитки; к основному цвету стен — ещё 2 соседних оттенка. Красить только в цвет утверждённого выкраса.
2. Краску заказывать по коду из графы «Система и код цвета» у бренда этого кода, не «аналогом» другого; весь объём одного кода — одной партией, колеруемую краску — за один проход машины.
3. Площади — те же, что в ведомости отделки (лист С1); сколько краски заказать — в спецификации отделочных материалов (лист С2).

Схема квартиры: цвет стен и акценты (б/м)

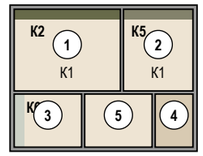


Схема палитры проекта


Стиль: Джапанди · схема: аналоговая

основной	основной	второстепенный	второстепенный	второстепенный	акцентный	акцентный	акцентный
NCS S 0804-Y30R	**Tikkurila F485**	**Tikkurila X447**	**Tikkurila V484**	**NCS S 2005-Y30R**	**Farrow & Ball No. 298**	**NCS S 5010-G70Y**	**NCS S 7005-Y20R**
светлый «рисовая бумага» LRV 78 стены 1,2,3,5; плинтус 1,2,3,5	Damask LRV 83 потолок 1,2,3,4,5; текстиль/декор 1,2,3,4	Sea Smoke LRV 63 акцент 3; текстиль/декор 1,2,3	Driftwood LRV 47 текстиль/декор 1,2,3	песочный грейж LRV 55 текстиль/декор 2,4	Bancha LRV ≈14 акцент 1; текстиль/декор 1	приглушённая олива LRV 22 акцент 2; текстиль/декор 2,4	тёмный орех LRV 9 в отделке не применён

План 60/30/10



Окраска, факт — по площади стен, акцентов, потолков

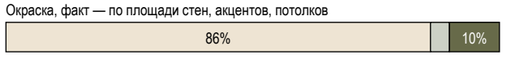

окрашено всего 169,3 м²; второстепенный тон несут мебель и текстиль

Текстиль и декор в цветах вне палитры проекта

NCS S 1002-Y50R тёплый светлый грейж — пом. 3 (Т10)

Условные обозначения

K1 NCS S 0804-Y30R · светлый «рисовая бумага» · Tikkurila Euro Power 7, колеровка по NCS · матовая · кл. 1

K2 Farrow & Ball No. 298 · Bancha · Modern Emulsion · матовая · кл. 1

K3 Tikkurila F485 · Damask · Euro Power 7 · глубокомат. · кл. 2

K4 NCS S 0804-Y30R · светлый «рисовая бумага» · МДФ

K5 NCS S 5010-G70Y · приглушённая олива · Tikkurila Euro Power 7, колеровка по NCS · матовая · кл. 1

K6 Tikkurila X447 · Sea Smoke · Euro Power 7 · матовая · кл. 1

K7 NCS S 0804-Y30R · светлый «рисовая бумага» · Orac Decor Contour (Luxxus)

K8 Tikkurila F485 · Damask · Euro Power 7 · матовая · кл. 1

дерево (доска, паркет, ламинат) — рисунок досок

керамогранит, плитка, камень — сетка швов по формату

KM1 инженерная доска · 1167-1101

KM2 аналог: керамогранит под травертин, матовый, 1200×600×9 мм

KM3 плитка · A8UZ


KM4 аналог: керамогранит ректифицированный под травертин, матовый, 600×600×9 мм

KM5 керамогранит · A8UZ

K — краска, KM — отделочный материал (тон KM — по описанию, эталон — образец материала); кл. — класс истирания (1 — самый стойкий к мытью); LRV — светлота цвета: 0 — чёрный, 100 — белый; «≈» — ориентировочно

	Лист	№ док.	Подпись	Дата	Проект: Квартира 56 м²			
Дизайнер	Кырлан А.С.			13.11.26	Колерная карта	Стадия	Лист	Листов
Проверил						П	19	92
Н. контр.								
Утв.								

выпуск 13.11.2026 № 568a382a0d · стр. 19 из 92

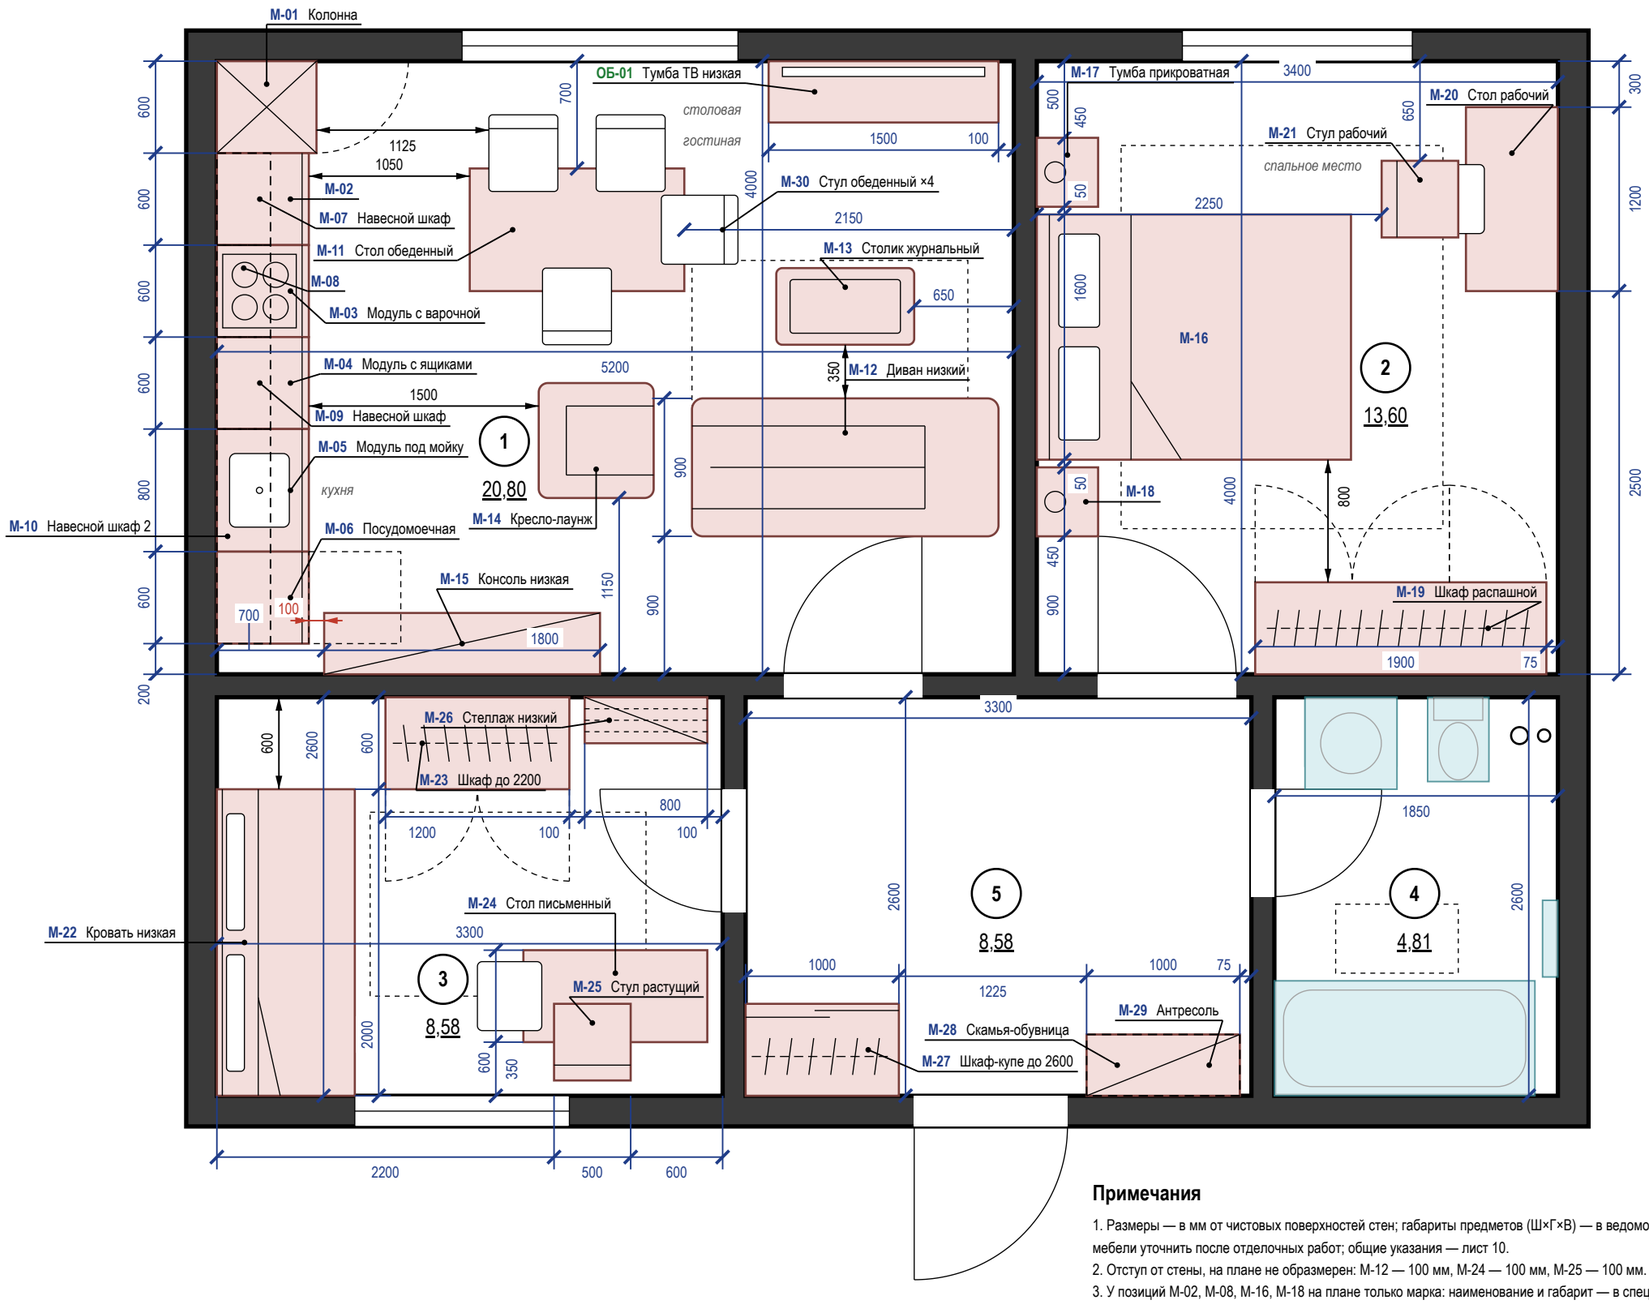

Экспликация помещений

лист 12 · на плане — номера в марках

Ведомость мебели и оборудования

Марка	Наименование	Ш×Г×В, мм	Пом.	Кол.
М-01	Колонна с холодильником встроенным	600×650×2350	1	1
М-02	Модуль с ящиками	600×600×900	1	1
М-03	Модуль с варочной панелью	600×600×900	1	1
М-04	Модуль с ящиками	600×600×900	1	1
М-05	Модуль под мойку	800×600×900	1	1
М-06	Посудомоечная машина встроенная 600	600×600×900	1	1
М-07	Навесной шкаф	600×350×900	1	1
М-08	Вытяжка встроенная в навесной шкаф	600×350×800	1	1
М-09	Навесной шкаф	600×350×900	1	1
М-10	Навесной шкаф 2 секции	1400×350×900	1	1
М-11	Стол обеденный 1400×800	1400×800×740	1	1
ОБ-01	Тумба ТВ низкая	1500×400×450	1	1
М-12	Диван низкий 2000×900	900×2000×750	1	1
М-13	Столик журнальный низкий	900×500×350	1	1
М-14	Кресло-лаунж	750×750×750	1	1
М-15	Консоль низкая 1800×400	1800×400×700	1	1
М-16	Кровать-подиум 1600×2000	1600×2050×900	2	1
М-17	Тумба прикроватная	450×400×400	2	1
М-18	Тумба прикроватная	450×400×400	2	1
М-19	Шкаф распашной 1900×600 до 2400	1900×600×2400	2	1
М-20	Стол рабочий у окна 1200×600	1200×600×750	2	1
М-21	Стул рабочий	500×500×800	2	1
М-22	Кровать 900×2000 низкая	2000×900×700	3	1
М-23	Шкаф 1200×600 до 2200	1200×600×2200	3	1
М-24	Стол письменный растущий 1200×600	600×1200×700	3	1
М-25	Стул растущий	500×500×800	3	1
М-26	Стеллаж низкий для книг	800×300×1200	3	1
М-27	Шкаф-купе 1000×600 до 2600	1000×600×2510	5	1
М-28	Скамья-обувница 1000×400	1000×400×450	5	1
М-29	Антресоль над скамьёй 1000×400	1000×400×500	5	1
М-30	Стул обеденный к столу М-11	450×500×820	1	4

Ш — вдоль стены (изголовья), Г — от стены (длина кровати)

Материалы, модели, допуск замены — лист 21

Примечания

1. Размеры — в мм от чистовых поверхностей стен; габариты предметов (Ш×Г×В) — в ведомости мебели, лист 21, на плане марка и короткое имя; размеры мебели уточнить после отделочных работ; общие указания — лист 10.
2. Отступ от стены, на плане не образмерен: М-12 — 100 мм, М-24 — 100 мм, М-25 — 100 мм.
3. У позиций М-02, М-08, М-16, М-18 на плане только марка: наименование и габарит — в спецификации, лист 21.
4. Стулья обеденной группы (М-30 — 4 шт.) показаны в рабочем положении, задвинутыми под столешницу на 150 мм.

	Лист	№ док.	Подпись	Дата	Проект: Квартира 56 м²			М 1:40
Дизайнер	Кырлан А.С.			13.11.26	План размещения мебели и оборудования	Стадия	Лист	Листов
Проверил						П	20	92
Н. контр.								
Утв.								

выпуск 13.11.2026 № 568a382a0d · стр. 20 из 92

Поз.	Наименование и техническая характеристика	Тип, марка, обозначение документа, опросного листа	Код продукции	Поставщик	Ед. измерения	Кол.	Масса 1 ед., кг	Примечание
	Мебель встроенная и корпусная (изготовление по чертежам мебельщика)							
М-01	Колонна с холодильником встроенным, фасад — дуб рифлёный; корпус ЛДСП 16 мм; фасады — МДФ 18 мм, эмаль матовая; цвет фасадов — в цвет стен (NCS S 0804-Y30R); Ш×Г×В 600×650×2350 мм	—	—	изготовление на заказ	шт.	1	—	пом. 1; крепление к стене
М-02	Модуль с ящиками; корпус ЛДСП 16 мм; фасады — МДФ 18 мм, эмаль матовая; цвет фасадов — в цвет стен (NCS S 0804-Y30R); Ш×Г×В 600×600×900 мм	—	—	изготовление на заказ	шт.	1	—	пом. 1
М-03	Модуль с варочной панелью и духовым шкафом; корпус ЛДСП 16 мм; фасады — МДФ 18 мм, эмаль матовая; цвет фасадов в цвет стен (NCS S 0804-Y30R); Ш×Г×В 600×600×900 мм	—	—	изготовление на заказ	шт.	1	—	пом. 1
М-04	Модуль с ящиками; корпус ЛДСП 16 мм; фасады — МДФ 18 мм, эмаль матовая; цвет фасадов — в цвет стен (NCS S 0804-Y30R); Ш×Г×В 600×600×900 мм	—	—	изготовление на заказ	шт.	1	—	пом. 1
М-05	Модуль под мойку; корпус ЛДСП 16 мм; фасады — МДФ 18 мм, эмаль матовая; цвет фасадов — в цвет стен (NCS S 0804-Y30R); Ш×Г×В 800×600×900 мм	—	—	изготовление на заказ	шт.	1	—	пом. 1
М-06	Модуль под встраиваемую ПММ 60; без корпуса (ниша между соседними модулями); фасад на дверь машины — МДФ 18 мм, эмаль матовая; цоколь; цвет фасадов — в цвет стен (NCS S 0804-Y30R); Ш×Г×В 600×600×900 мм	—	—	изготовление на заказ	шт.	1	—	пом. 1
М-07	Навесной шкаф, фасад — дуб рифлёный; корпус ЛДСП 16 мм; фасады — МДФ 18 мм, эмаль матовая; цвет фасадов — в цвет стен (NCS S 0804-Y30R); Ш×Г×В 600×350×900 мм	—	—	изготовление на заказ	шт.	1	—	пом. 1
М-08	Вытяжка встроенная в навесной шкаф, рециркуляция до обмера вентканала; корпус ЛДСП 16 мм; фасады — МДФ 18 мм, эмаль матовая; цвет фасадов — в цвет стен (NCS S 0804-Y30R); Ш×Г×В 600×350×800 мм	—	—	изготовление на заказ	шт.	1	—	пом. 1
М-09	Навесной шкаф; корпус ЛДСП 16 мм; фасады — МДФ 18 мм, эмаль матовая; цвет фасадов — в цвет стен (NCS S 0804-Y30R); Ш×Г×В 600×350×900 мм	—	—	изготовление на заказ	шт.	1	—	пом. 1
М-10	Навесной шкаф 2 секции, с сушкой; корпус ЛДСП 16 мм; фасады — МДФ 18 мм, эмаль матовая; цвет фасадов — в цвет стен (NCS S 0804-Y30R); Ш×Г×В 1400×350×900 мм	—	—	изготовление на заказ	шт.	1	—	пом. 1
М-19	Шкаф распашной 1900×600 до 2400, фасады — дуб рифлёный; корпус ЛДСП 16 мм; фасады — МДФ 18 мм, эмаль матовая; цвет фасадов — в цвет стен (NCS S 0804-Y30R); Ш×Г×В 1900×600×2400 мм	—	—	изготовление на заказ	шт.	1	—	пом. 2; крепление к стене
М-23	Шкаф 1200×600 до 2200, фасады — дуб и серо-зелёный; корпус ЛДСП 16 мм; фасады — МДФ 18 мм, эмаль матовая; цвет фасадов — в цвет стен (NCS S 0804-Y30R); Ш×Г×В 1200×600×2200 мм	—	—	изготовление на заказ	шт.	1	—	пом. 3; крепление к стене
М-27	Шкаф-купе 1000×600 до 2600, двери — дуб и зеркало; корпус ЛДСП 16 мм; фасады — ЛДСП 10 мм, декор «дуб натуральный» в профиле: алюминий, чёрный матовый; вставка — зеркало серебро 4 мм, плёнка безопасности; Ш×Г×В 1000×600×2510 мм	—	—	изготовление на заказ	шт.	1	—	пом. 5
М-29	Антресоль над скамьёй 1000×400, фасад в цвет стены; каркас и полки — ЛДСП 16 мм, декор «дуб натуральный»; без фасадов; Ш×Г×В 1000×400×500 мм	—	—	изготовление на заказ	шт.	1	—	пом. 5; крепление к стене
	Мебель покупная							
М-11	Стол обеденный 1400×800, массив дуба, низкие стулья Wishbone; шпон, дуб натуральный, матовое масло; Ш×Г×В 1400×800×740 мм	аналог: Ш×Г×В 1400×800×740 мм, шпон	—	аналог по характеристикам	шт.	1	—	пом. 1; замена ≤ габарита
М-12	Диван низкий 2000×900, лён, сиденье 400; обивка — ткань, цвет Tikkurila X447; Ш×Г×В 900×2000×750 мм	аналог: Ш×Г×В 900×2000×750 мм, обивка — ткань	—	аналог по характеристикам	шт.	1	—	пом. 1; замена ≤ габарита
М-13	Столик журнальный низкий, массив дуба; шпон, дуб натуральный, матовое масло; Ш×Г×В 900×500×350 мм	аналог: Ш×Г×В 900×500×350 мм, шпон	—	аналог по характеристикам	шт.	1	—	пом. 1; замена ≤ габарита
М-14	Кресло-лаунж, тёмный ясень и шерсть; обивка — ткань, цвет Tikkurila X447; Ш×Г×В 750×750×750 мм	аналог: Ш×Г×В 750×750×750 мм, обивка — ткань	—	аналог по характеристикам	шт.	1	—	пом. 1; замена ≤ габарита
М-15	Консоль низкая 1800×400, тёмный ясень, фасады рифлёные; шпон, дуб натуральный, матовое масло; Ш×Г×В 1800×400×700 мм	аналог: Ш×Г×В 1800×400×700 мм, шпон	—	аналог по характеристикам	шт.	1	—	пом. 1; крепление к стене; замена ≤ габарита
М-30	Стул обеденный к столу М-11; обивка — ткань, цвет Tikkurila X447; каркас — дуб натуральный; Ш×Г×В 450×500×820 мм	аналог: Ш×Г×В 450×500×820 мм, обивка — ткань	—	аналог по характеристикам	шт.	4	—	пом. 1; замена ≤ габарита
ОБ-01	Тумба ТВ низкая, дуб, ТВ 55" шпон, дуб натуральный, матовое масло; Ш×Г×В 1500×400×450 мм	аналог: Ш×Г×В 1500×400×450 мм, шпон	—	аналог по характеристикам	шт.	1	—	пом. 1; замена ≤ габарита
М-16	Кровать-подиум 1600×2000, дуб, изголовье 900; мягкое изголовье, обивка — ткань, цвет Tikkurila X447; Ш×Г×В 1600×2050×900 мм	аналог: Ш×Г×В 1600×2050×900 мм, мягкое изголовье	—	аналог по характеристикам	шт.	1	—	пом. 2; замена ≤ габарита
М-17, М-18	Тумба прикроватная, дуб; шпон, дуб натуральный, матовое масло; Ш×Г×В 450×400×400 мм	аналог: Ш×Г×В 450×400×400 мм, шпон	—	аналог по характеристикам	шт.	2	—	пом. 2; замена ≤ габарита

Примечания

1. Позиции мебели совпадают с марками на плане расстановки; размеры Ш×Г×В — Ш вдоль стены, Г от стены.
2. Размеры и привязки плана расстановки — в мм от чистовых поверхностей стен: слой штукатурки 20 мм по блоку и 5 мм шпаклёвки по ГКЛ учтён; привязки — от стен и углов помещения, а не от другой мебели.
3. План расстановки не является документацией для изготовления мебели. Встроенная и корпусная мебель изготавливается по чертежам мебельщика после контрольного обмера (после штукатурки); «стена в стену» — с зазором 10 мм с каждой стороны или с компенсаторами; графы «Тип, марка» и «Код продукции» для неё не заполняются (ГОСТ 21.110-2013).
4. Покупные изделия — аналог по характеристикам: заменять только на изделия не больше указанного габарита и того же материала и цвета.
5. Материал и цвет, не указанные в данных изделия, приняты по концепции: тон дерева — по полу, обивка — по вторичному цвету палитры; образцы согласовать до заказа.
6. Масса 1 ед. для изделий до 25 кг не указывается. Техника — по монтажным схемам изготовителя; выводы — по листам ЭОМ и ВК.

	Лист	№ док.	Подпись	Дата	Проект: Квартира 56 м²			
Дизайнер	Кырлан А.С.			13.11.26	Спецификация мебели и оборудования	Стадия	Лист	Листов
Проверил						П	21	92
Н. контр.								
Утв.								

выпуск 13.11.2026 № 568a382a0d · стр. 21 из 92

Поз.	Наименование и техническая характеристика	Тип, марка, обозначение документа, опросного листа	Код продукции	Поставщик	Ед. измерения	Кол.	Масса 1 ед., кг	Примечание
М-20	Стол рабочий у окна 1200×600, дуб (работа из дома); шпон, дуб натуральный, матовое масло; Ш×Г×В 1200×600×750 мм	аналог: Ш×Г×В 1200×600×750 мм, шпон	—	аналог по характеристикам	шт.	1	—	пом. 2; замена ≤ габарита
М-21	Стул рабочий, гнутая фанера; обивка — ткань, цвет Tikkurila X447; каркас — дуб натуральный; Ш×Г×В 500×500×800 мм	аналог: Ш×Г×В 500×500×800 мм, обивка — ткань	—	аналог по характеристикам	шт.	1	—	пом. 2; замена ≤ габарита
М-22	Кровать 900×2000 низкая, дуб, спинка-бортик 700 вдоль стены; мягкое изголовье, обивка — ткань, цвет Tikkurila X447; Ш×Г×В 2000×900×700 мм	аналог: Ш×Г×В 2000×900×700 мм, мягкое изголовье	—	аналог по характеристикам	шт.	1	—	пом. 3; замена ≤ габарита
М-24	Стол письменный растущий 1200×600; шпон, дуб натуральный, матовое масло; Ш×Г×В 600×1200×700 мм	аналог: Ш×Г×В 600×1200×700 мм, шпон	—	аналог по характеристикам	шт.	1	—	пом. 3; замена ≤ габарита
М-25	Стул растущий; обивка — ткань, цвет Tikkurila X447; каркас — дуб натуральный; Ш×Г×В 500×500×800 мм	аналог: Ш×Г×В 500×500×800 мм, обивка — ткань	—	аналог по характеристикам	шт.	1	—	пом. 3; замена ≤ габарита
М-26	Стеллаж низкий для книг и игрушек 800×300; шпон, дуб натуральный, матовое масло; Ш×Г×В 800×300×1200 мм	аналог: Ш×Г×В 800×300×1200 мм, шпон	—	аналог по характеристикам	шт.	1	—	пом. 3; крепление к стене; замена ≤ габарита
М-28	Скамья-обувница 1000×400, дуб; Ш×Г×В 1000×400×450 мм	аналог: Ш×Г×В 1000×400×450 мм	—	аналог по характеристикам	шт.	1	—	пом. 5; замена ≤ габарита
	Техника встраиваемая и бытовая (покупные изделия), светильники под розетки							
	Холодильник встраиваемый, в модуле М-01	аналог по характеристикам: полновстраиваемый под фасад, ниша 1780 × 560 × 550 мм, вентиляция решётка в цоколе, выход сверху	—	по выбору заказчика до изготовления мебели	шт.	1	—	пом. 1; по схеме изготовителя
	Посудомоечная машина встраиваемая, в модуле М-06; ниша 600 мм	аналог по характеристикам: полновстраиваемая 60 см под фасад, ниша 600 × 862 мм, навеска фасада в комплекте	—	по выбору заказчика до изготовления мебели	шт.	1	—	пом. 1; по схеме изготовителя
	Вытяжка встраиваемая, в модуле М-08	аналог по характеристикам: производительность — по расчёту ОВ, шум ≤ 55 дБ(А)	—	по выбору заказчика до изготовления мебели	шт.	1	—	пом. 1; по схеме изготовителя
	Варочная панель встраиваемая, индукционная, в модуле М-03	аналог по характеристикам: индукционная 60 см, вырез 560 × 490 мм по шаблону модели	—	по выбору заказчика до изготовления мебели	шт.	1	—	пом. 1; по схеме изготовителя
	Духовой шкаф встраиваемый, в модуле М-03	аналог по характеристикам: 60 см, лицевая панель 595 мм, ниша 560 × 600, глубина ≥ 550 мм, вентиляция за прибором	—	по выбору заказчика до изготовления мебели	шт.	1	—	пом. 1; по схеме изготовителя
	Стиральная машина, место по листу ВК (ОБ-03); Ш×Г 600×600 мм	аналог по характеристикам: тип загрузки — по листу ВК, в плане 600 × 600 мм (ширина × глубина), по листу ВК	—	по выбору заказчика до изготовления мебели	шт.	1	—	пом. 4; по схеме изготовителя
	Торшер, у поз. М-12; абажур — ткань или опаловое стекло; лампа 2700 K	—	—	аналог по характеристикам	шт.	1	—	пом. 1; розетка Р21 (ЭОМ)
	Торшер, у поз. М-18; абажур — ткань или опаловое стекло; лампа 2700 K	—	—	аналог по характеристикам	шт.	1	—	пом. 2; розетка Р5 (ЭОМ)
	Текстиль							
Т13	Портьеры-волна (гостиная); лён 70 %, вискоза 30 %; цвет Tikkurila X447; карниз 2250 мм, высота 2690 мм, сборка 2	—	—	аналог по характеристикам	шт.	2	—	пом. 1
Т14	Тюль (гостиная); полиэстер 100 %; цвет Tikkurila F485; карниз 2250 мм, высота 2690 мм, сборка 2,5	—	—	аналог по характеристикам	шт.	1	—	пом. 1
Т16	Ковёр в зоне отдыха, джут с шерстью; шерсть 100 %; цвет Tikkurila V484; 1800×1600 мм	—	—	аналог по характеристикам	шт.	1	—	пом. 1; с подложкой
Т17	Подушки на диван; букле (шерсть 60 %, полиэстер 40 %); цвет Tikkurila X447	—	—	аналог по характеристикам	шт.	2	—	пом. 1
Т18	Подушки на диван, акцент; хлопковый бархат 100 %; цвет Farrow & Ball No. 298	—	—	аналог по характеристикам	шт.	2	—	пом. 1
Т19	Плед на диван; альпака 50 %, шерсть 50 %; цвет Tikkurila V484	—	—	аналог по характеристикам	шт.	1	—	пом. 1
Т1	Портьеры-волна; лён 100 %; цвет Tikkurila X447; карниз 2500 мм, высота 2590 мм, сборка 2	—	—	аналог по характеристикам	шт.	2	—	пом. 2
Т2	Тюль; полиэстер 100 %; цвет Tikkurila F485; карниз 2500 мм, высота 2590 мм, сборка 2,5	—	—	аналог по характеристикам	шт.	1	—	пом. 2
Т3	Ковёр под кроватью, шерсть; шерсть 80 %, хлопок 20 %; цвет NCS S 2005-Y30R; 2100×2500 мм	—	—	аналог по характеристикам	шт.	1	—	пом. 2; с подложкой
Т4	Подушки декоративные на кровать; лён 100 %; цвет Tikkurila X447	—	—	аналог по характеристикам	шт.	2	—	пом. 2
Т5	Подушки на кровать, акцент; хлопковый бархат 100 %; цвет NCS S 5010-G70Y	—	—	аналог по характеристикам	шт.	2	—	пом. 2

	Лист	№ док.	Подпись	Дата
Дизайнер	Кырлан А.С.			13.11.26
Проверил				
Н. контр.				
Утв.				

Проект: Квартира 56 м²

Спецификация мебели и оборудования (продолжение)

Стадия	Лист	Листов
П	22	92

Поз.	Наименование и техническая характеристика	Тип, марка, обозначение документа, опросного листа	Код продукции	Поставщик	Ед. измерения	Кол.	Масса 1 ед., кг	Примечание
Т6	Плед на кровать; шерсть мериноса 100 %; цвет NCS S 5010-G70Y	—	—	аналог по характеристикам	шт.	1	—	пом. 2
Т7	Портьеры-волна; лён 100 %; цвет Tikkurila X447; карниз 1820 мм, высота 2590 мм, сборка 2	—	—	аналог по характеристикам	шт.	2	—	пом. 3
Т8	Тюль; полиэстер 100 %; цвет Tikkurila F485; карниз 1820 мм, высота 2590 мм, сборка 2,5	—	—	аналог по характеристикам	шт.	1	—	пом. 3
Т9	Ковёр игровой, шерсть; шерсть 100 %; цвет Tikkurila V484; 1800×1200 мм	—	—	аналог по характеристикам	шт.	1	—	пом. 3; с подложкой
Т10	Подушки декоративные на кровать; букле (шерсть 60 %, полиэстер 40 %); цвет NCS S 1002-Y50R	—	—	аналог по характеристикам	шт.	2	—	пом. 3
Т11	Подушки на кровать, акцент; хлопковый бархат 100 %; цвет Tikkurila X447	—	—	аналог по характеристикам	шт.	2	—	пом. 3
Т12	Плед на кровать; шерсть мериноса 100 %; цвет Tikkurila X447	—	—	аналог по характеристикам	шт.	1	—	пом. 3
Т20	Полотенца банные махровые, приглушённая олива, сложены на полотенцесушителе; хлопок 100 %; цвет NCS S 5010-G70Y	—	—	аналог по характеристикам	шт.	2	—	пом. 4
Т21	Полотенца для рук вафельные, тёплый белый, на нижних перекладинах сушителя; хлопок 100 %; цвет Tikkurila F485	—	—	аналог по характеристикам	шт.	2	—	пом. 4
Т22	Ковёр — коврик для ванной у бортика ванны, хлопок тафтинг, песочный; хлопок 100 %, латексная противоскользящая основа; цвет NCS S 2005-Y30R; 800×450 мм	—	—	аналог по характеристикам	шт.	1	—	пом. 4; с подложкой
	Декор							
ДК6	Картина над консолью: горный ручей, тушь суми-э, рама — тёмный ясень; 1000×700 мм; низ на 950 мм от пола	—	—	аналог по характеристикам	шт.	1	6	пом. 1; крепление: анкер, 2 шт.
ДК7	Фикус каучуконосный в кашпо Ø450, глина; 450×450 мм	—	—	аналог по характеристикам	шт.	1	—	пом. 1
ДК8	Ваза керамическая с одной веткой на обеденном столе; 200×350 мм; на М-11	—	—	аналог по характеристикам	шт.	1	—	пом. 1
ДК11	Книги стопкой и свеча в керамической чаше на журнальном столике; 300×130 мм; на М-13	—	—	аналог по характеристикам	шт.	1	—	пом. 1
ДК12	Вазы ручной работы разной высоты (340 и 220 мм), 2 шт., оливковая глазурь, на консоли М-15; 250×340 мм; на М-15	—	—	аналог по характеристикам	шт.	2	—	пом. 1
ДК13	Лампа настольная на консоли М-15: основание — тёмный ясень, абажур — рисовая бумага; 220×480 мм; на М-15	—	—	аналог по характеристикам	шт.	1	—	пом. 1
ДК14	Чаши ручной работы, 2 шт., и чайник, оливковая глазурь, на столешнице кухни; 280×220 мм; на М-04	—	—	аналог по характеристикам	шт.	2	—	пом. 1
ДК1	Картина над кроватью: ветка сакуры, акварель, паспарту, рама — дуб; 1000×700 мм; низ на 1100 мм от пола	—	—	аналог по характеристикам	шт.	1	4	пом. 2; крепление к стене
ДС1	Реечная панель: дуб, за изголовьем кровати; низ на 80 мм от пола	—	—	аналог по характеристикам	шт.	1	—	пом. 2
ДК15	Книги стопкой на тумбе М-17; 250×120 мм; на М-17	—	—	аналог по характеристикам	шт.	1	—	пом. 2
ДК16	Шеффлера в глиняном кашпо Ø350; 380×380 мм	—	—	аналог по характеристикам	шт.	1	—	пом. 2
ДК17	Лампа настольная рабочая на столе М-20: стойка — дуб, абажур-колпак — рисовая бумага; 220×480 мм; на М-20	—	—	аналог по характеристикам	шт.	1	—	пом. 2
ДК3	Картина над кроватью: кот на подоконнике, детская иллюстрация, рама — светлый дуб; 1200×600 мм; низ на 900 мм от пола	—	—	аналог по характеристикам	шт.	1	4	пом. 3; крепление к стене
ДК4	Зеркало в рост в тонкой чёрной раме; рама — чёрный матовый; 500×1500 мм; низ на 300 мм от пола	—	—	аналог по характеристикам	шт.	1	12	пом. 3; крепление: анкер для пустотелых оснований, 4 шт.
ДК18	Лампа настольная рабочая на столе М-24: шарнирная стойка — светлый дуб, абажур-колпак серо-зелёный; 220×480 мм; на М-24	—	—	аналог по характеристикам	шт.	1	—	пом. 3
ДК2	Зеркало над умывальником, влагостойкое, с подсветкой; 600×800 мм; низ на 1200 мм от пола	—	—	аналог по характеристикам	шт.	1	—	пом. 4
ДК9	Ваза-бутыль керамическая, приглушённая олива, с сухой веткой эвкалипта — на полке короба инсталляции; 130×400 мм	—	—	аналог по характеристикам	шт.	1	—	пом. 4
ДК5	Зеркало над скамьёй, тонкая чёрная рама; рама — чёрный матовый; 600×1200 мм; низ на 700 мм от пола	—	—	аналог по характеристикам	шт.	1	18	пом. 5; крепление: анкер, 4 шт.
ДК10	Графика в раме из тёмного ясеня 400×560: энсо — круг одним движением кисти, тушь; 400×560 мм; низ на 1220 мм от пола	—	—	аналог по характеристикам	шт.	1	2	пом. 5; крепление: дюбель с крюком, 2 точки

	Лист	№ док.	Подпись	Дата
Дизайнер	Кырлан А.С.			13.11.26
Проверил				
Н. контр.				
Утв.				

Проект: Квартира 56 м²

Спецификация мебели и оборудования (продолжение)

Стадия	Лист	Листов
П	23	92

Ведомость изделий

Марка	Наименование	Пом.	Ш×Г×В, мм	Корпус	Фасад	Кромка, мм	Кол.
М-19	Шкаф распашной	2	1900×600×2400	ЛДСП 16	МДФ 18 мм, эмаль матовая	0,4 / 2	1
М-23	Шкаф распашной	3	1200×600×2200	ЛДСП 16	МДФ 18 мм, эмаль матовая	0,4 / 2	1
М-27	Шкаф-купе	5	1000×600×2510	ЛДСП 16	ЛДСП 10 мм, декор «дуб натуральный» в профиле: алюминий, чёрный матовый; вставка — зеркало серебро 4 мм, плёнка безопасности	0,4 / 2	1
М-29	Система хранения	5	1000×400×500	ЛДСП 16	без фасадов	0,4 / 2	1
М-06	Модуль под ПММ 60: без корпуса, фасад на дверь машины	1	600×600×900	без корпуса	МДФ 18 мм, эмаль матовая — на дверь машины (навеска из её комплекта), цоколь		1
М-10	Модуль навесной: полки, сушка	1	1400×350×900	ЛДСП 16	МДФ 18 мм, эмаль матовая	0,4 / 2	1
М-05	Модуль нижний: мойка	1	800×600×900	ЛДСП 16	МДФ 18 мм, эмаль матовая	0,4 / 2	1
М-04	Модуль нижний: ящики	1	600×600×900	ЛДСП 16	МДФ 18 мм, эмаль матовая	0,4 / 2	1
М-09	Модуль навесной: полки	1	600×350×900	ЛДСП 16	МДФ 18 мм, эмаль матовая	0,4 / 2	1
М-03	Модуль нижний: духовой шкаф, варочная	1	600×600×900	ЛДСП 16	МДФ 18 мм, эмаль матовая	0,4 / 2	1
М-08	Модуль навесной: полки	1	600×350×800	ЛДСП 16	МДФ 18 мм, эмаль матовая	0,4 / 2	1
М-02	Модуль нижний: ящики	1	600×600×900	ЛДСП 16	МДФ 18 мм, эмаль матовая	0,4 / 2	1
М-07	Модуль навесной: полки	1	600×350×900	ЛДСП 16	МДФ 18 мм, эмаль матовая	0,4 / 2	1
М-01	Пенал: холодильник встр.	1	600×650×2350	ЛДСП 16	МДФ 18 мм, эмаль матовая	0,4 / 2	1

Ведомость встраиваемой техники

Поз.	Прибор	Ниша, вырез, мм	Вентиляция	Питание	Схема
М-06	Посудомоечная машина встраиваемая, 60 см	ниша 600 × 862 (от пола до низа столешницы)	зазор в цоколе, по схеме	Р32: —, Н=300 — вне гарнитура	по модели
М-05	Мойка врезная / подстольная с сифоном	вырез по шаблону, ориентир 700 × 480		смеситель — выводы ВК	по модели
М-03	Духовой шкаф встраиваемый, 60 см	ниша 560 × 600, глубина ≥ 550	зазор за шкафом, вырез в задней стенке	ЭВ2: М-03, Н=150 — под духовым шкафом, доступ через ящик	по модели
М-03	Варочная панель индукционная, 60 см	вырез в столешнице 560 × 490		ЭВ1: М-04, Н=600 — в соседнем модуле, за ящиком	по модели
М-01	Холодильник встраиваемый, ниша 1780	ниша 1780 × 560 × 550	решётка в цоколе, канал за корпусом, выход сверху	Р25: М-01, Н=2120 — над нишей холодильника, съёмная панель	по модели
М-08	Вытяжка встраиваемая в навесной модуль, 60 см	низ ≥ 650 над панелью	воздуховод к вентканалу, короб до потолка	ЭВ3: М-08, Н=2200 — в навесном модуле	по модели

Ведомость фурнитуры

№	Фурнитура	Тип, размер	Изделия	Кол.
1	Петля накладная 110° с доводчиком	чашка 35 мм	М-19, М-23, М-10, М-05, М-09, М-08, М-07, М-01	73
2	Полкодержатель с фиксацией	ø5 мм	М-19, М-23, М-27, М-10, М-09, М-08, М-07, М-01	96
3	Штанга овальная 30×15, L = 926	+ 2 держателя	М-19	1
4	Опора регулируемая с цоколем на клипсах	ход 20 мм	М-19, М-23, М-27	20
5	Анкер по основанию стены	по таблице крепежа	М-19, М-23, М-27, М-29, М-10, М-09, М-08, М-07	28
6	Уголок крепления к стене от опрокидывания	стальной	М-19, М-23, М-27, М-29, М-01	10
7	Штанга овальная 30×15, L = 776	+ 2 держателя	М-23	1
8	Система дверей купе: профиль, направляющие, ролики	на 2 двери	М-27	1
9	Ручка-профиль вертикальная	в цвет профиля	М-27	2
10	Штанга овальная 30×15, L = 476	+ 2 держателя	М-27	1
11	Полка для обуви выдвижная наклонная	ширина 476	М-27, М-29	7
12	Ручка-профиль	латунь матовая	М-06, М-10, М-05, М-04, М-09, М-03, М-08, М-02, М-07, М-01	23
13	Комплект навески фасада ПММ	из поставки машины	М-06	1
14	Сушка для посуды в шкаф	ширина 800	М-10	1
15	Навес регулируемый для навесного шкафа	пара на секцию	М-10, М-09, М-08, М-07	5
16	Шина монтажная	L = 1340	М-10	1
17	Опора кухонная регулируемая 100–120 мм	+ клипса цоколя	М-05, М-04, М-03, М-02, М-01	22
18	Направляющие полного выдвижения с доводчиком NL 500	пара	М-04, М-03, М-02	7
19	Шина монтажная	L = 540	М-09, М-08, М-07	3


Примечания

1. Модели техники выбирает заказчик до изготовления мебели; ниши, вырезы и вентиляция — по монтажной схеме выбранной модели (условие гарантии), её номер вносится в ведомость.
2. Количество фурнитуры — по чертежам изделий; запас крепежа 5 %. Аналоги — по характеристикам (доводчик, нагрузка, ход).
3. Цвет корпусов, фасадов и профилей — по колерной карте проекта. Кромка — скрытые / видимые торцы, мм.


	Лист	№ док.	Подпись	Дата	Проект: Квартира 56 м²			
Дизайнер	Кырлан А.С.			13.11.26	Ведомости изделий, техники и фурнитуры	Стадия	Лист	Листов
Проверил						П	24	92
Н. контр.								
Утв.								

выпуск 13.11.2026 № 568a382a0d · стр. 24 из 92

Фрагмент 1. Гостиная-кухня, пом. 1 (М 1:20)

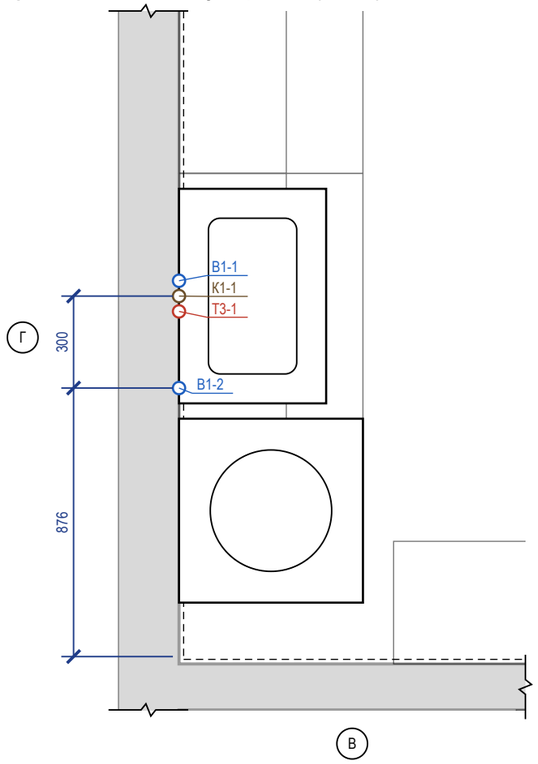

Фрагмент 2. Санузел, пом. 4 (М 1:20)

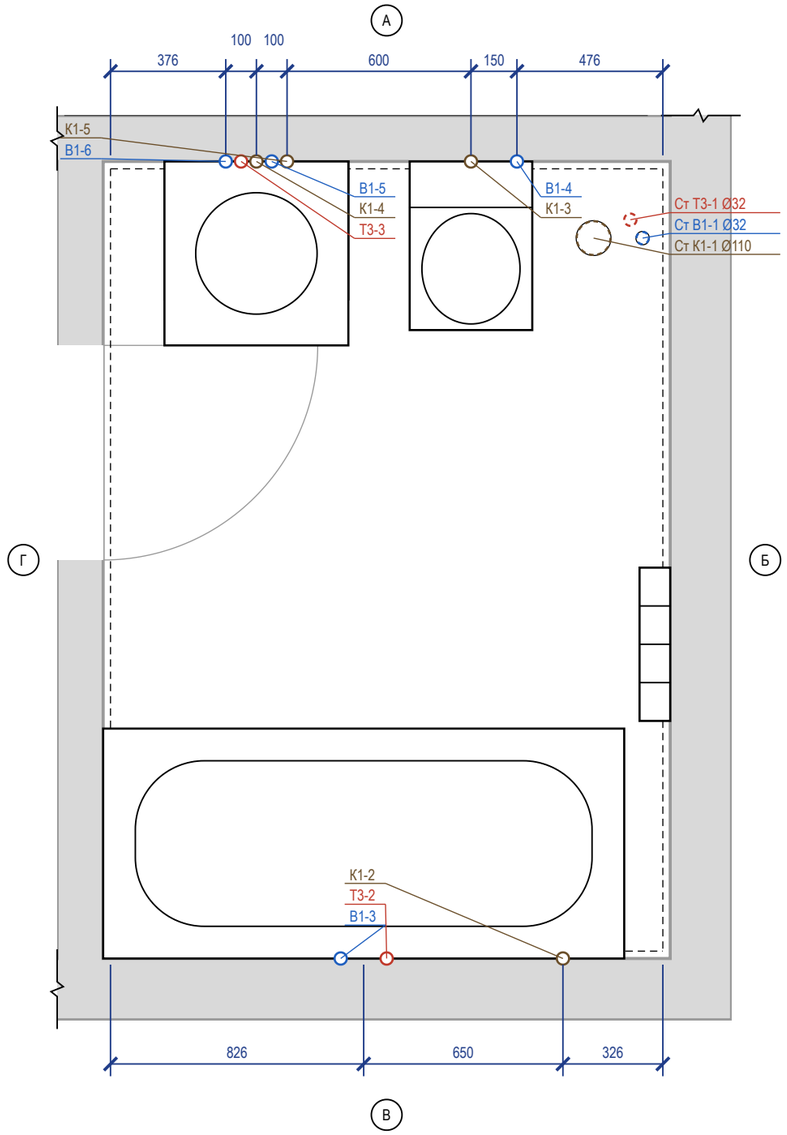

Ведомость привязок выводов

Код	Прибор	Ø	H, мм	Привязка от чист. стен, мм	Прим.
В1-1	С-01 мойка кухонная	½"	600	ст. Г: 1226 от В	межос. 100
Т3-1	—"	½"	600	ст. Г: 1126 от В	межос. 100
К1-1	—"	Ø50	400	ст. Г: 1176 от В	
В1-2	ОБ-02 посудомоечная машина	½"	550	ст. Г: 876 от В	кран ПММ в шкафу мойки
В1-3	С-02 ванна	½"	800	ст. В: 751 от Г	межос. 150
Т3-2	—"	½"	800	ст. В: 901 от Г	межос. 150
К1-2	—"	Ø50	50	ст. В: 326 от Б	
В1-4	С-03 унитаз подвесной	½"	250	ст. А: 476 от Б	в раме инсталляции
К1-3	—"	Ø110	220	ст. А: 626 от Б	
В1-5	С-04 умывальник	½"	950	ст. А: 526 от Г	межос. 100
Т3-3	—"	½"	950	ст. А: 426 от Г	межос. 100
К1-4	—"	Ø50	900	ст. А: 476 от Г	плоский сифон, над машиной
В1-6	ОБ-03 стиральная машина	½"	600	ст. А: 376 от Г	кран машины
К1-5	—"	Ø50	600	ст. А: 576 от Г	

Условные обозначения

- вывод В1 (код — в ведомости привязок)
- вывод Т3 (код — в ведомости привязок)
- вывод К1 (код — в ведомости привязок)
- сантехприбор по расстановке (габарит модели)
- чистовая поверхность стены (от неё привязки)
- стояк «Ст К1-N / Ст В1-N» (ГОСТ 21.601), Ø мм
- стояк Т3 не на обмере — принят в шахте рядом со Ст В1, сверить
- линия обрыва (граница фрагмента)
- А — обозначение стены А–Г (как на развёртках)

Примечания

1. Привязки выводов даны от чистовых поверхностей стен (облицовка на сторону: гостиная-кухня — 24 мм (фартук: штукатурка 10 + клей 5 + плитка 9); санузел — 24 мм (штукатурка 10 + клей 5 + плитка 9)); эти же грани — на развёртках и в раскладке плитки. Высоты — от чистого пола помещения.
2. До черновой разводки сверить по паспорту выбранного прибора (смеситель, инсталляция, сифон).
3. Горячая вода (Т3) — слева от холодной (В1), если смотреть на прибор. Допуск установки выводов: ±5 мм в группе, ±20 мм у отдельно стоящих.
4. Расчёт систем водоснабжения и канализации и подбор оборудования выполняет проектная организация; лист задаёт места и высоты выводов.
5. Посудомоечная машина ОБ-02: кран — отдельным выводом в шкафу мойки, слив — в отвод сифона мойки С-01 (своего выпуска нет), шланг с петлёй выше сифона.
6. Раковина над стиральной машиной С-04: плоский сифон, водорозетки и выпуск — над корпусом машины (высоты в таблице), не за ней.
7. Ст К1-1, Ст В1-1, Ст Т3-1 на обмере не показаны: приняты рядом с Ст В1-1 (в МКД стоят группой); положение сверить на объекте до разметки.
8. Стояки в коробах/шахтах не замоноличивать; стояк К1 в коробе — звукоизоляция стояка в коробе без жёсткого контакта с трубой; к арматуре и ревизиям — люк не меньше 300×400.

	Лист	№ док.	Подпись	Дата
Дизайнер	Кырлан А.С.			13.11.26
Проверил				
Н. контр.				
Утв.				


Проект: Квартира 56 м² — **М 1:20**

План выводов сантехники


Стадия	Лист	Листов
П	25	92

выпуск 13.11.2026 № 568a382a0d · стр. 25 из 92


План квартиры (М 1:200)

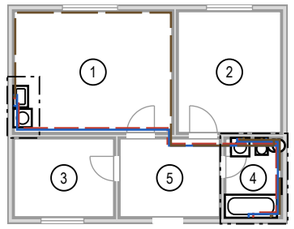

Фр. 1. Гостиная-кухня (М 1:25)

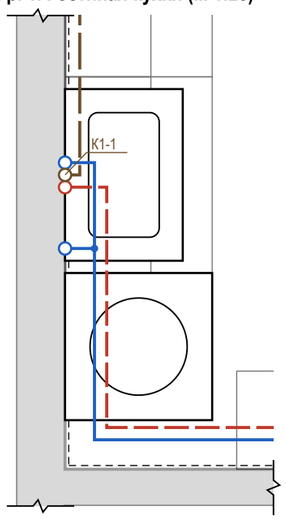

Фр. 2. Санузел (М 1:25)

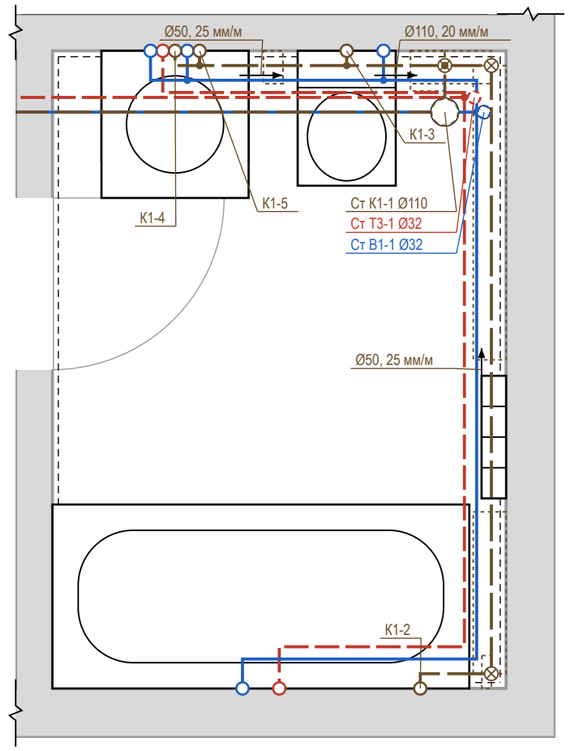

Условные обозначения

- В1 — водопровод хозяйственно-питьевой (ХВС), PP-R Ø20
- Т3 — горячее водоснабжение, подача (ГВС), PP-R Ø20
- К1 — канализация бытовая
- направление уклона К1 / пола: Ø, мм на 1 м
- ревизия (прочистка) К1 — доступ сохранить
- тройник (ответвление к прибору)
- короб К1 над чистым полом (ГКЛВ под плитку)
- вывод В1 (код — в ведомости привязок)
- вывод Т3 (код — в ведомости привязок)
- вывод К1 (код — в ведомости привязок)
- сантехприбор по расстановке (габарит модели)
- стояк «Ст К1-N / Ст В1-N» (ГОСТ 21.601), Ø мм
- стояк Т3 не на обмере — принят в шахте рядом со Ст В1, сверить
- линия обрыва (граница фрагмента)
- граница фрагмента на плане (Фр. N)

Профиль выпусков К1 (до врезки в стояк)

Выпуск	Прибор	Ø	L, м	i, мм/м	Δh, мм	Прокладка, мм
К1-3	С-03 унитаз подвесной	Ø110	0,65	20	13	короб 160×140
К1-1	С-01 мойка кухонная	Ø50	15,58	25	390	через пом. 5: короба нет; до решения
К1-2	С-02 ванна	Ø50	3,21	25	80	короб 160×110
К1-4	С-04 умывальник	Ø50	1,35	25	34	короб 120×110
К1-5	ОБ-03 стиральная машина	Ø50	1,25	25	31	короб 120×110

Короб h×b: h — от чистого пола, b — от чистовой стены. Стяжка 35 мм — лист полов.

Узел ввода В1, Т3 (схема, без масштаба)



состав узла — по согласованию

⊗ Ст К1-1: ревизия на стояке — люк в коробе


Примечания

1. Трассы принципиальные, построены от стояков вдоль стен помещений; фактическое положение фиксируется исполнительной схемой с привязками (фото с рулеткой) до закрытия.
2. Уклон К1 не менее 1/d и не более 150 мм/м (СП 30.13330.2020, п. 19.1), приняты практические уклоны; поворот — двумя отводами 45°, ревизия после поворота, доступ сохранить. Стояк К1 в коробе — звукоизоляция стояка в коробе, без жёсткого контакта короба с трубой.
3. Решение по К1: стяжка 35 мм не укрывает трубы (нужно Ø + Δh + 45 мм) — выпуски идут над чистым полом вдоль стен; К1-3, К1-2, К1-4, К1-5 — в коробе ГКЛВ под плитку (размеры в профиле). Короба — на развёртках; отметку низа врезки в стояк замерить до черновых работ.
4. К1-1 (С-01 мойка кухонная): до Ст К1-1 15,58 м через пом. 5, перепад 390 мм — короб 470×110 через чужие помещения не построить: насосная установка (КНС) у прибора, подиум или прибор ближе к стояку — решение заказчика; до решения не выполнять.
5. Состав узла ввода В1, Т3 — по согласованию: на схеме типовой узел — кран шаровой, фильтр, счётчик, обратный клапан, кран; состав и места не определены (записи реестра нет). Доступ к арматуре — через люк не меньше 300×400. Водопровод — в штробе стен или в коробах; трубы испытать давлением до закрытия (акт скрытых работ).
6. Расчёт систем, диаметры магистралей и подбор оборудования выполняет проектная организация; врезка и перенос стояков — по согласованию с управляющей организацией. Арматуру и привязки сверить по паспортам приборов.
7. Ведомость выводов (код, прибор, высота, привязка) — лист 25; на схеме — только коды.
8. Ст К1-1, Ст В1-1, Ст Т3-1 на обмере не показаны: приняты рядом с Ст В1-1 (в МКД стоят группой); положение сверить на объекте до разводки.

	Лист	№ док.	Подпись	Дата	Проект: Квартира 56 м²			
Дизайнер	Кырлан А.С.			13.11.26	Схема разводки водопровода и канализации	Стадия	Лист	Листов
Проверил						П	26	92
Н. контр.								
Утв.								

выпуск 13.11.2026 № 568a382a0d · стр. 26 из 92

Схема В1 (М 1:50)

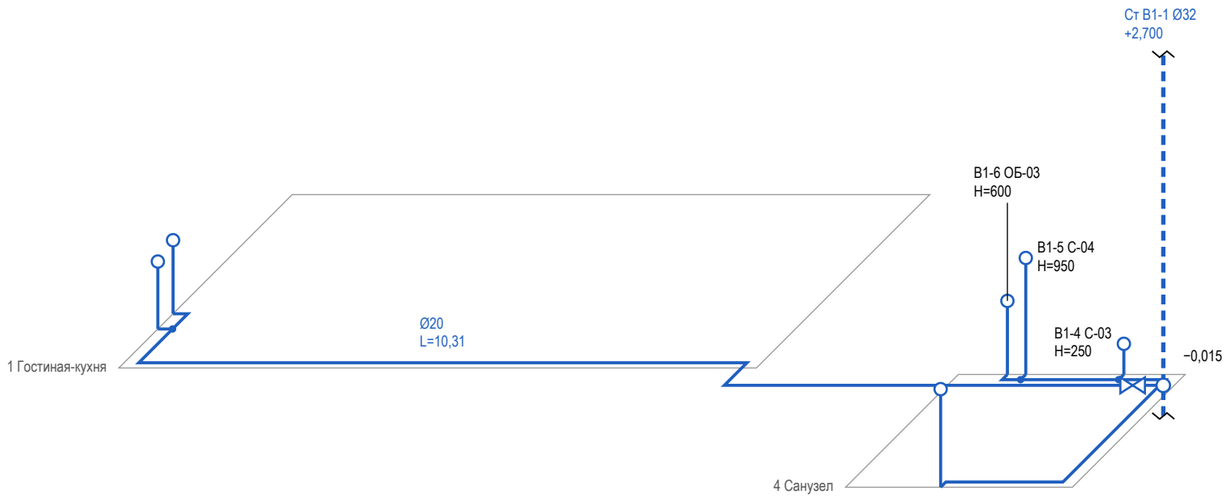

Ведомость выводов В1

Код	Прибор	H, мм	Ø, мм	Трасса, м
В1-1	С-01 мойка кухонная	600	20	10,31
В1-2	ОБ-02 посудомоечная машина	550	20	0,12
В1-3	С-02 ванна	800	20	3,31
В1-6	ОБ-03 стиральная машина	600	20	1,58
В1-5	С-04 умывальник	950	20	0,12
В1-4	С-03 унитаз подвесной	250	20	0,12

Условные обозначения

- В1 — водопровод хозяйственно-питьевой (ХВС), PP-R Ø20
- вывод В1 (код — в ведомости привязок)
- стояк «Ст К1-N / Ст В1-N» (ГОСТ 21.601), Ø мм
- стояк в плане (на отметке пола); вертикаль — стояк по высоте, разрыв — перекрытие
- тройник (ответвление к прибору)
- кран шаровой
- стояк Т3 не на обмере — принят в шахте рядом со Ст В1, сверить

Примечания

1. Схема В1 построена по тем же трассам, что план разводки: положение в плане сохранено, глубина — в масштабе ×0,5. Трассы принципиальные; фактическое положение фиксируется исполнительной схемой до закрытия.
2. Высоты H — от чистого пола помещения, мм. Отметка прокладки магистрали В1 (в стяжке, в стене или по полу) в данных не задана: участки показаны на уровне пола условно (записи реестра нет).
3. Узел ввода В1 (кран, фильтр, счётчик, обратный клапан, кран) — на схеме разводки; состав узла ввода — по согласованию. Кран шаровой — на первом участке от стояка.
4. Ст В1-1 на обмере не показаны: положение принято (по брифу заказчика), не замерено; положение сверить на объекте до разводки.
5. Трубы испытать давлением до закрытия (акт скрытых работ, опрессовка по СП 73.13330.2016).
6. Диаметры, высоты выводов и места кранов — по паспортам выбранных приборов и расчёту проектной организации.
7. Расчёт систем, диаметры магистралей и подбор оборудования выполняет проектная организация.

	Лист	№ док.	Подпись	Дата
Дизайнер	Кырлан А.С.			13.11.26
Проверил				
Н. контр.				
Утв.				


Проект: Квартира 56 м² — **М 1:50**

Аксонометрическая схема В1 (холодное водоснабжение)

Стадия	Лист	Листов
П	27	92

выпуск 13.11.2026 № 568a382a0d · стр. 27 из 92

Схема Т3 (М 1:50)

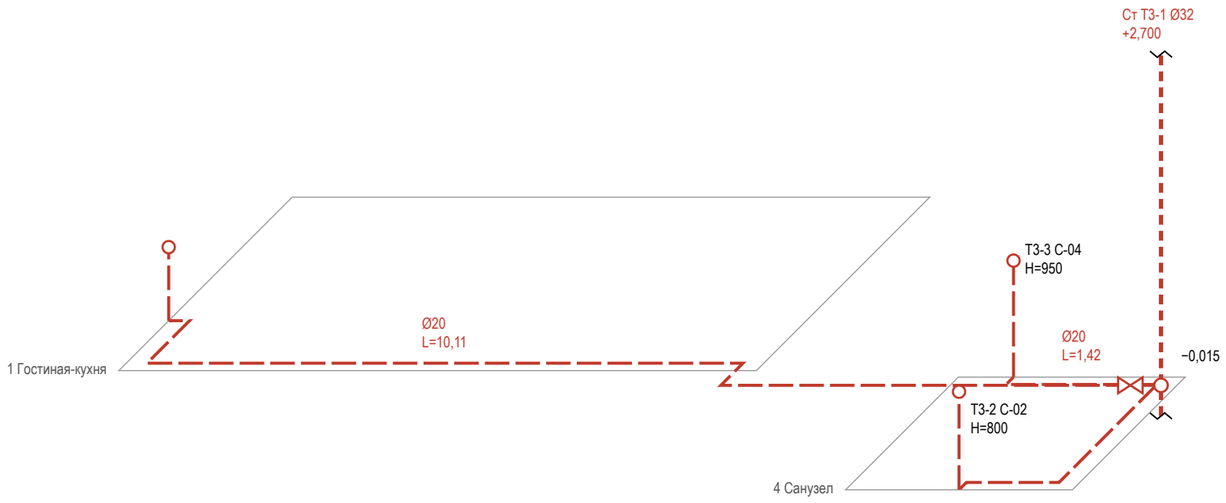

Ведомость выводов Т3

Код	Прибор	H, мм	Ø, мм	Трасса, м
Т3-1	С-01 мойка кухонная	600	20	10,11
Т3-2	С-02 ванна	800	20	3,17
Т3-3	С-04 умывальник	950	20	1,42

Условные обозначения

- Т3 — горячее водоснабжение, подача (ГВС), PP-R Ø20
- вывод Т3 (код — в ведомости привязок)
- стояк «Ст К1-N / Ст В1-N» (ГОСТ 21.601), Ø мм
- стояк в плане (на отметке пола); вертикаль — стояк по высоте, разрыв — перекрытие
- тройник (ответвление к прибору)
- кран шаровой
- стояк Т3 не на обмере — принят в шахте рядом со Ст В1, сверить


Примечания

1. Схема Т3 построена по тем же трассам, что план разводки: положение в плане сохранено, глубина — в масштабе ×0,5. Трассы принципиальные; фактическое положение фиксируется исполнительной схемой до закрытия.
2. Высоты H — от чистого пола помещения, мм. Отметка прокладки магистрали Т3 (в стяжке, в стене или по полу) в данных не задана: участки показаны на уровне пола условно (записи реестра нет).
3. Узел ввода Т3 (кран, фильтр, счётчик, обратный клапан, кран) — на схеме разводки; состав узла ввода — по согласованию. Кран шаровой — на первом участке от стояка.
4. Циркуляция ГВС в данных не задана — циркуляционного трубопровода на схеме нет (записи реестра нет).
5. Ст Т3-1 на обмере не показаны: приняты рядом с Ст В1-1 (в МКД стоят группой); положение сверить на объекте до разводки.
6. Трубы испытать давлением до закрытия (акт скрытых работ, опрессовка по СП 73.13330.2016).
7. Диаметры, высоты выводов и места кранов — по паспортам выбранных приборов и расчёту проектной организации.
8. Расчёт систем, диаметры магистралей и подбор оборудования выполняет проектная организация.

	Лист	№ док.	Подпись	Дата	Проект: Квартира 56 м²	М 1:50		
Дизайнер	Кырлан А.С.			13.11.26	Аксонометрическая схема Т3 (горячее водоснабжение)	Стадия	Лист	Листов
Проверил						П	28	92
Н. контр.								
Утв.								

выпуск 13.11.2026 № 568a382a0d · стр. 28 из 92

Схема К1 (М 1:50)

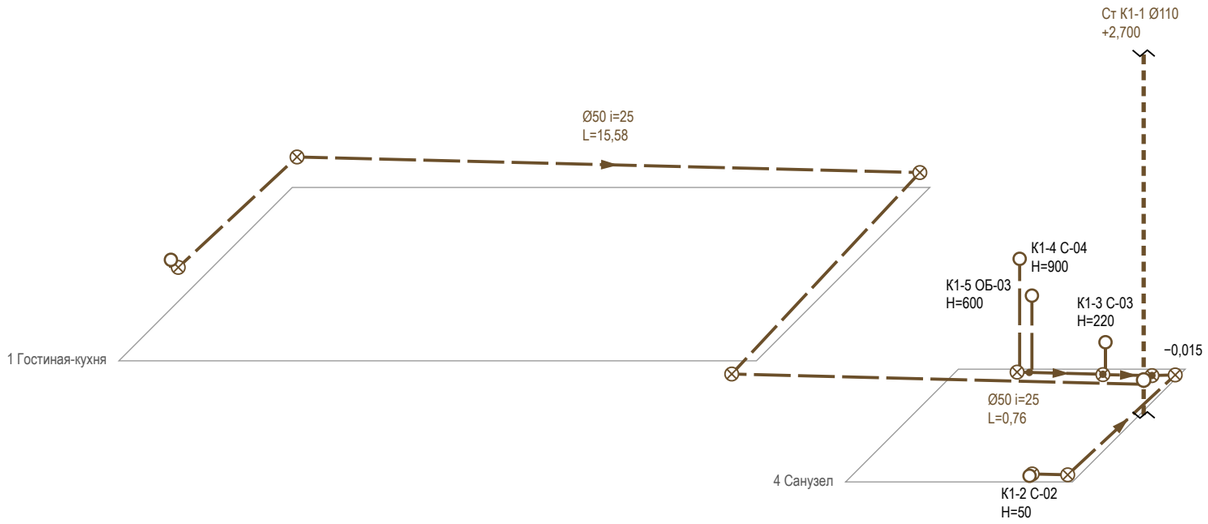

Ведомость выводов К1

Код	Прибор	H, мм	Ø, i	Трасса, м
К1-3	С-03 унитаз подвесной	220	110 i=20	0,65
К1-1	С-01 мойка кухонная	400	50 i=25	15,58
К1-2	С-02 ванна	50	50 i=25	3,02
К1-4	С-04 умывальник	900	50 i=25	0,76
К1-5	ОБ-03 стиральная машина	600	50 i=25	0,06

Условные обозначения

- К1 — канализация бытовая
- вывод К1 (код — в ведомости привязок)
- стояк «Ст К1-N / Ст В1-N» (ГОСТ 21.601), Ø мм
- стояк в плане (на отметке пола); вертикаль — стояк по высоте, разрыв — перекрытие
- направление уклона К1 / пола: Ø, мм на 1 м
- ревизия (прочистка) К1 — доступ сохранить
- тройник (ответвление к прибору)
- стояк Т3 не на обмере — принят в шахте рядом со Ст В1, сверить


Примечания

1. Схема К1 построена по тем же трассам, что план разводки: положение в плане сохранено, глубина — в масштабе ×0,5. Трассы принципиальные; фактическое положение фиксируется исполнительной схемой до закрытия.
2. Отметки — от плиты перекрытия: низ трубы у врезки в стояк — отметка из данных выпуска, к прибору труба поднимается на уклон i, мм/м (уклон не менее 1/d и не более 150 мм/м, СП 30.13330.2020, п. 19.1); чистый пол — выше плиты на стяжку (высота пирога пола). Высота выпуска прибора H — от чистого пола.
3. Ревизия — на повороте и в начале участка; стояк К1 в коробе с люком — звукоизоляция стояка в коробе; поворот — двумя отводами 45°.
4. Ст К1-1 на обмере не показаны: положение принято (по брифу заказчика), не замерено; положение сверить на объекте до разводки.
5. Трубы испытать давлением до закрытия (акт скрытых работ, опрессовка по СП 73.13330.2016).
6. Диаметры, высоты выводов и места кранов — по паспортам выбранных приборов и расчёту проектной организации.
7. Расчёт систем, диаметры магистралей и подбор оборудования выполняет проектная организация.

	Лист	№ док.	Подпись	Дата	Проект: Квартира 56 м²	М 1:50		
Дизайнер	Кырлан А.С.			13.11.26	Аксонометрическая схема К1 (канализация)	Стадия	Лист	Листов
Проверил						П	29	92
Н. контр.								
Утв.								

выпуск 13.11.2026 № 568a382a0d · стр. 29 из 92

Стена Г (М 1:20)

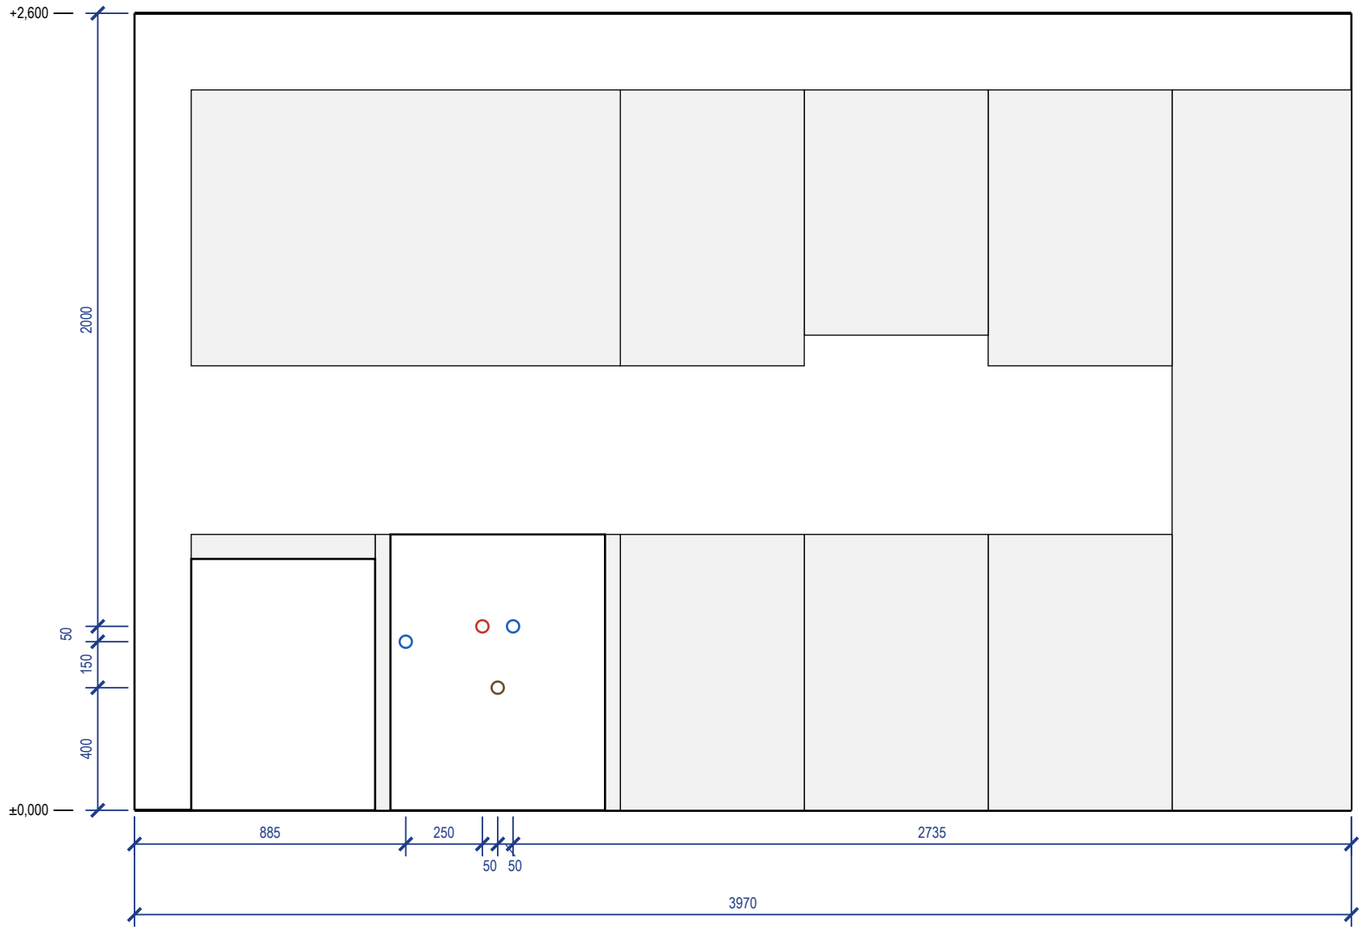

Ведомость привязок выводов (от чистого пола и угла)

Код	Прибор	Ø	H, мм	Привязка, мм
В1-1	С-01 мойка кухонная	½"	600	ст. Г: 1235 от лев. угла
Т3-1	С-01 мойка кухонная	½"	600	ст. Г: 1135 от лев. угла
К1-1	С-01 мойка кухонная	Ø50	400	ст. Г: 1185 от лев. угла
В1-2	ОБ-02 посудомоечная машина	½"	550	ст. Г: 885 от лев. угла

Условные обозначения

- вывод В1 (код — в ведомости привязок)
- вывод Т3 (код — в ведомости привязок)
- вывод К1 (код — в ведомости привязок)
- сантехприбор по расстановке (габарит модели)
- дверной проём; окно — сплошной контур


Примечания

1. Габариты и высоты приборов, межосевые смесителей и места кранов — по паспортам выбранных приборов, сверяются до разметки стен.
2. Высоты H — от чистого пола помещения, мм; отметка чистого пола и потолка — у левого края вида (от ±0,000 объекта). Привязки — от левого чистового угла вида (облицовка стен вычтена), как на развёртках стен.
3. Ревизионные люки к арматуре и ревизиям в данных не заданы: место и размер не определены (записи реестра нет).
4. Мойка, ПММ и фильтр — выводы в шкафу мойки; диаметры и положение сифона и кранов сверить по паспортам приборов и чертежам модуля.
5. Часть подписей выводов не уместилась у знака: коды и высоты — в ведомости привязок.
6. Расчёт систем водоснабжения и канализации и подбор оборудования выполняет проектная организация; лист задаёт места и высоты выводов.


	Лист	№ док.	Подпись	Дата	Проект: Квартира 56 м²	М 1:20
Дизайнер	Кырлан А.С.			13.11.26		
Проверил					Развёртки мокрых зон: выводы ВК. Гостиная-кухня	Стадия: П; Лист: 30; Листов: 92
Н. контр.						
Утв.						

выпуск 13.11.2026 № 568a382a0d · стр. 30 из 92

Стена А (М 1:20)

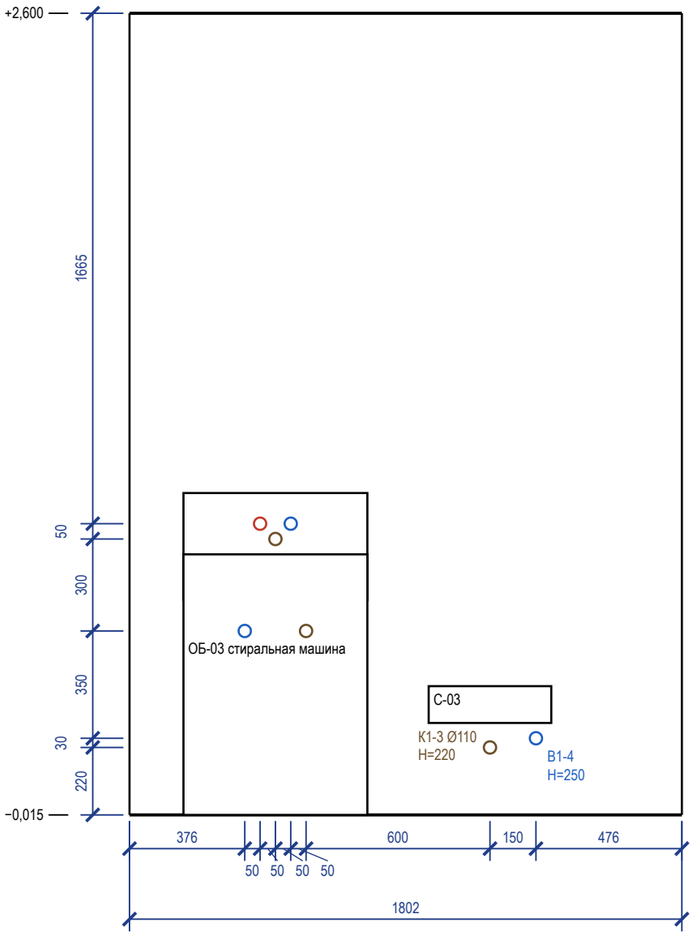

Стена В (М 1:20)

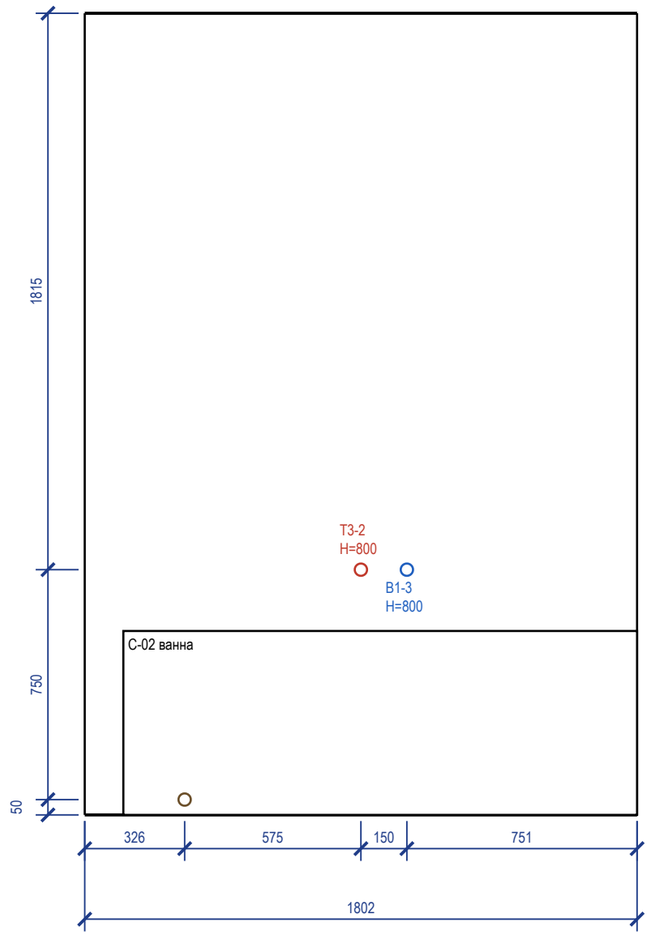

Ведомость привязок выводов (от чистого пола и угла)

Код	Прибор	Ø	H, мм	Привязка, мм
В1-4	С-03 унитаз подвесной	½"	250	ст. А: 1326 от лев. угла
К1-3	С-03 унитаз подвесной	Ø110	220	ст. А: 1176 от лев. угла
В1-5	С-04 умывальник	½"	950	ст. А: 526 от лев. угла
Т3-3	С-04 умывальник	½"	950	ст. А: 426 от лев. угла
К1-4	С-04 умывальник	Ø50	900	ст. А: 476 от лев. угла

Ведомость привязок (продолжение)

Код	Прибор	Ø	H, мм	Привязка, мм
В1-6	ОБ-03 стиральная машина	½"	600	ст. А: 376 от лев. угла
К1-5	ОБ-03 стиральная машина	Ø50	600	ст. А: 576 от лев. угла
В1-3	С-02 ванна	½"	800	ст. В: 1051 от лев. угла
Т3-2	С-02 ванна	½"	800	ст. В: 901 от лев. угла
К1-2	С-02 ванна	Ø50	50	ст. В: 326 от лев. угла

Условные обозначения

- вывод В1 (код — в ведомости привязок)
- вывод Т3 (код — в ведомости привязок)
- вывод К1 (код — в ведомости привязок)
- сантехприбор по расстановке (габарит модели)
- дверной проём; окно — сплошной контур

Примечания

1. Габариты и высоты приборов, межосевые смесителей и места кранов — по паспортам выбранных приборов, сверяются до разметки стен.
2. Высоты H — от чистого пола помещения, мм; отметка чистого пола и потолка — у левого края вида (от ±0,000 объекта). Привязки — от левого чистового угла вида (облицовка стен вычтена), как на развёртках стен.
3. Стояки в помещении: Ст К1-1 Ø110, Ст В1-1 Ø32, Ст Т3-1 Ø32 — положение на плане выводов; выводы подключаются к ним по схеме разводки.
4. Ревизионные люки к арматуре и ревизиям в данных не заданы: место и размер не определены (записи реестра нет).
5. Часть подписей выводов не уместилась у знака: коды и высоты — в ведомости привязок.
6. Стены Б, Г: выводов В1, Т3, К1 нет — развёртка не строится (иначе лист-продолжение); приборы и проёмы этих стен — на плане выводов и развёртках стен чертёжника.
7. Расчёт систем водоснабжения и канализации и подбор оборудования выполняет проектная организация; лист задаёт места и высоты выводов.

	Лист	№ док.	Подпись	Дата	Проект: Квартира 56 м²	М 1:20		
Дизайнер	Кырлан А.С.			13.11.26	Развёртки мокрых зон: выводы ВК. Санузел	Стадия	Лист	Листов
Проверил						П	31	92
Н. контр.								
Утв.								

выпуск 13.11.2026 № 568a382a0d · стр. 31 из 92


Поз.	Наименование и техническая характеристика	Тип, марка, обозначение документа	Код продукции	Поставщик	Ед. изм.	Кол.	Масса 1 ед., кг	Примечание
	Санитарные приборы							
1	Ванна встраиваемая акриловая 1700×750 мм, с каркасом, экраном и отверстием слив-перелив	акриловая 1700×750, смеситель настенный		выбор заказчика	шт	1		С-02
2	Унитаз подвесной безободковый, с сиденьем микролифт, крепёж и звукоизолирующая прокладка	Laufen Pro 8.2096.6.000.000.1		выбор заказчика	шт	1		С-03
3	Инсталляция для подвесного унитаза: рама высотой 1120 мм, бачок, клавиша смыва (ось клавиши 1050 мм от чистого пола)	аналог		выбор заказчика	шт	1		С-03; короб ГКЛВ
4	Раковина над стиральной машиной 600×450 мм, плоская, с переливом и выпуском под плоский сифон	аналог		выбор заказчика	шт	1		С-04
5	Мойка врезная, нержавеющая сталь, чёрная 700×480 мм, с переливом	аналог		с кухонной мебелью	шт	1		С-01
6	Полотенцесушитель электрический, IP44, с терморегулятором	аналог		выбор заказчика	шт	1		С-05
	Смесители, сифоны и арматура приборов							
7	Смеситель для ванны настенный однорычажный, межосевое 150 мм, с душевым набором (лейка, шланг, держатель)	аналог		выбор заказчика	шт	1		С-02
8	Смеситель для умывальника однорычажный, с донным клапаном	аналог		выбор заказчика	шт	1		С-04
9	Смеситель кухонный однорычажный, высокий излив	аналог		выбор заказчика	шт	1		С-01
10	Обвязка ванны слив-перелив Ø40/50 с сифоном	аналог		выбор заказчика	шт	1		С-02
11	Сифон плоский для раковины над стиральной машиной Ø32/40–50, выпуск в стену над корпусом машины	аналог		выбор заказчика	шт	1		С-04
12	Сифон для мойки с отводом для ПММ Ø40/50	аналог		выбор заказчика	шт	1		С-01; слив ОБ-02
13	Сифон для стиральной машины встраиваемый в стену Ø50, с обратным клапаном	аналог		выбор заказчика	шт	1		ОБ-03
14	Кран угловой ½"×½" с гибкой подводкой 40 см (умывальники, мойка)	аналог		выбор заказчика	шт	4		по 2 на прибор
15	Кран шаровой угловой ½"×¾" для подключения стиральной и посудомоечной машины	аналог		выбор заказчика	шт	2		ОБ-03, ОБ-02
	Трубопроводы							
16	Труба полипропиленовая PP-R PN20 Ø20×3,4 (В1)	ГОСТ 32415-2013		выбор заказчика	м	21,5	0,17	15,6 + 3,8 + 10 %
17	Труба PP-R, армированная стекловолокном, PN20 Ø20×2,8 (Т3)	ГОСТ 32415-2013		выбор заказчика	м	19	0,15	14,7 + 2,4 + 10 %
18	Труба канализационная ПП Ø50 (К1)	ГОСТ 32414-2013		выбор заказчика	м	24		19,4 + 1,9 + 10 %
19	Труба канализационная ПП Ø110 (К1)	ГОСТ 32414-2013		выбор заказчика	м	1		0,7 + 0,2 + 10 %
	Фасонные части и выводы							
20	Отвод канализационный ПП 45° Ø50	ГОСТ 32414-2013		выбор заказчика	шт	16		2 шт. на поворот
21	Отвод канализационный ПП 45° Ø110	ГОСТ 32414-2013		выбор заказчика	шт	4		2 шт. на поворот
22	Тройник канализационный ПП 45° (врезки ветвей)	ГОСТ 32414-2013		выбор заказчика	шт	4		
23	Ревизия канализационная ПП (после поворота трассы)	ГОСТ 32414-2013		выбор заказчика	шт	6		доступ сохранить
24	Фитинги PP-R Ø20: тройники, угольники 90° (ветви и повороты В1, Т3)	ГОСТ 32415-2013		выбор заказчика	шт	23		
25	Водорозетка PP-R Ø20×½" настенная, с креплением	ГОСТ 32415-2013		выбор заказчика	шт	9		коды — лист выводов
	Узлы ввода, люки, короба							
26	Кран шаровой латунный Ду15 PN16 (отключение ввода)	аналог		выбор заказчика	шт	2		Ст В1-1, Ст Т3-1
27	Фильтр сетчатый косой Ду15	аналог		выбор заказчика	шт	2		
28	Счётчик воды крыльчатый Ду15 (ХВ, ГВ), с поверкой	аналог		выбор заказчика	шт	2		пломба УК
29	Клапан обратный Ду15	аналог		выбор заказчика	шт	2		
30	Люк ревизионный нажимной под плитку 300×400 мм	аналог		выбор заказчика	шт	1		к стоякам и арматуре
31	Звукоизоляция стояка К1 в коробе: рулонный звукоизоляционный материал ≥ 10 мм, обмотка стояка на высоту этажа	аналог		выбор заказчика	м	2,7		Ст К1-1
32	Короб К1 над полом: профиль ПН/ПС, ГКЛВ 12,5 мм под плитку	аналог		выбор заказчика	м	9,7		сечение — лист разводки

Примечания

1. Форма 1 ГОСТ 21.110-2013, ширины граф изменены по п. 4.1. «Аналог» — аналог по характеристикам: модели внести до черновых работ, привязки выводов сверить по паспортам.
2. Бытовая техника не входит (показана арматура подключения), мойка — в комплекте кухни (марка — модуля кухни, как у столяра). Длины труб — трасса листа разводки + подъёмы + 10 %.
3. Стояк К1 в коробе — звукоизоляция стояка в коробе без жёсткого контакта короба с трубой.
4. Расчёт систем водоснабжения и канализации, диаметры магистралей и подбор оборудования выполняет проектная организация.

	Лист	№ док.	Подпись	Дата	Проект: Квартира 56 м²			
Дизайнер	Кырлан А.С.			13.11.26				
Проверил					Спецификация сантехнического оборудования	Стадия	Лист	Листов
Н. контр.						П	32	92
Утв.								

выпуск 13.11.2026 № 568a382a0d · стр. 32 из 92

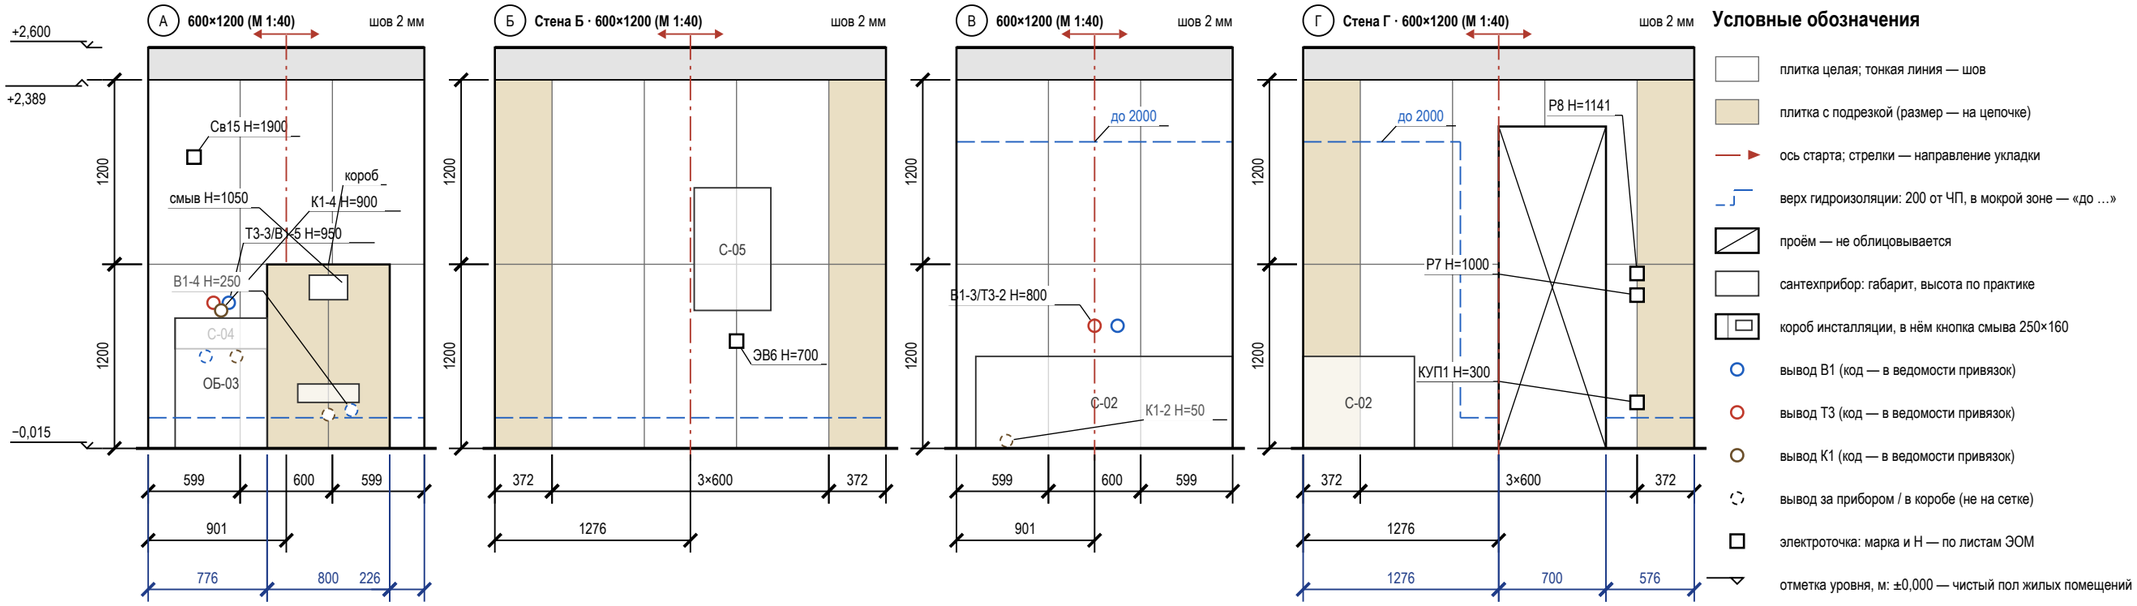

Условные обозначения

- плитка целая; тонкая линия — шов
- плитка с подрезкой (размер — на цепочке)
- ось старта; стрелки — направление укладки
- верх гидроизоляции: 200 от ЧП, в мокрой зоне — «до …»
- проём — не облицовывается
- сантехприбор: габарит, высота по практике
- короб инсталляции, в нём кнопка смыва 250×160
- вывод В1 (код — в ведомости привязок)
- вывод Т3 (код — в ведомости привязок)
- вывод К1 (код — в ведомости привязок)
- вывод за прибором / в коробе (не на сетке)
- электроточка: марка и Н — по листам ЭОМ
- отметка уровня, м: ±0,000 — чистый пол жилых помещений
- низ потолка; серая полоса — стена без плитки
- (А) обозначение стены А–Г (как на развёртках)

Подсчёт плитки по стенам и коробу


Поверхность	L × H, мм	S, м²	Целых	Подр.	С запасом	Подрезки: край / верх, мм
стена А	1802 × 2404	3,49	4	2	7	599 / 599; целый ряд
короб (ст. А)	800×1200×250	1,76	0	6	7	лицо 399 / 399; бок. 250
стена Б	2552 × 2404	6,25	6	4	11	372 / 372; целый ряд
стена В	1802 × 2404	4,45	6	0	7	599 / 599; целый ряд
стена Г	2552 × 2404	4,78	2	8	11	372 / 372; целый ряд
Итого		**20,73**	**18**	**20**	**43**	

Примечания

1. Вид изнутри, стены по часовой стрелке А → Г. Высоты — от чистого пола (−0,015), отметки — от ±0,000. Раскладка от чистовых размеров (штукатурка 10 + клей 5 + плитка 9 мм), подрезки чистые; старт — от оси стены, ряды от пола целыми.
2. Облицовка не до потолка: верх плитки +2,389, выше — отделка стены по ведомости отделки до потолка +2,600; торец облицовки — профиль-окантовка.
3. Открытые выводы и электроточки — на шве или в центре плитки (допуск 10 мм; плитка от 900 мм по высоте — на шве или не ближе 60 мм к нему).
4. Выводы ВК стоят по оси прибора и с прибором не двигаются — привязки по «Плану выводов сантехники» без сдвига; вне сетки (Т3-3/В1-5, К1-4, В1-3/Т3-2) — отверстие в плитке коронкой по той же привязке, плитку не сдвигать.
5. За приборами и в коробе (В1-4, К1-3, В1-6, К1-5, К1-2) — штриховым кольцом.
6. Гидроизоляция: 200 мм от ЧП по периметру; над ванной — до 2000 и 300 мм за борт (СП 29.13330.2011, п. 7.2 — на высоту замачивания); углы — лентой; акт скрытых работ, пролив.
7. Короб 800×1200×250: лицо 399 / 399 мм от оси кнопки смыва, боковины, полка; углы — запил 45° или профиль; за коробом плитку не кладут.

	Лист	№ док.	Подпись	Дата	Проект: Квартира 56 м²			М 1:40
Дизайнер	Кырлан А.С.			13.11.26	Раскладка плитки. Санузел. Развёртки стен	Стадия	Лист	Листов
Проверил						П	33	92
Н. контр.								
Утв.								

выпуск 13.11.2026 № 568a382a0d · стр. 33 из 92

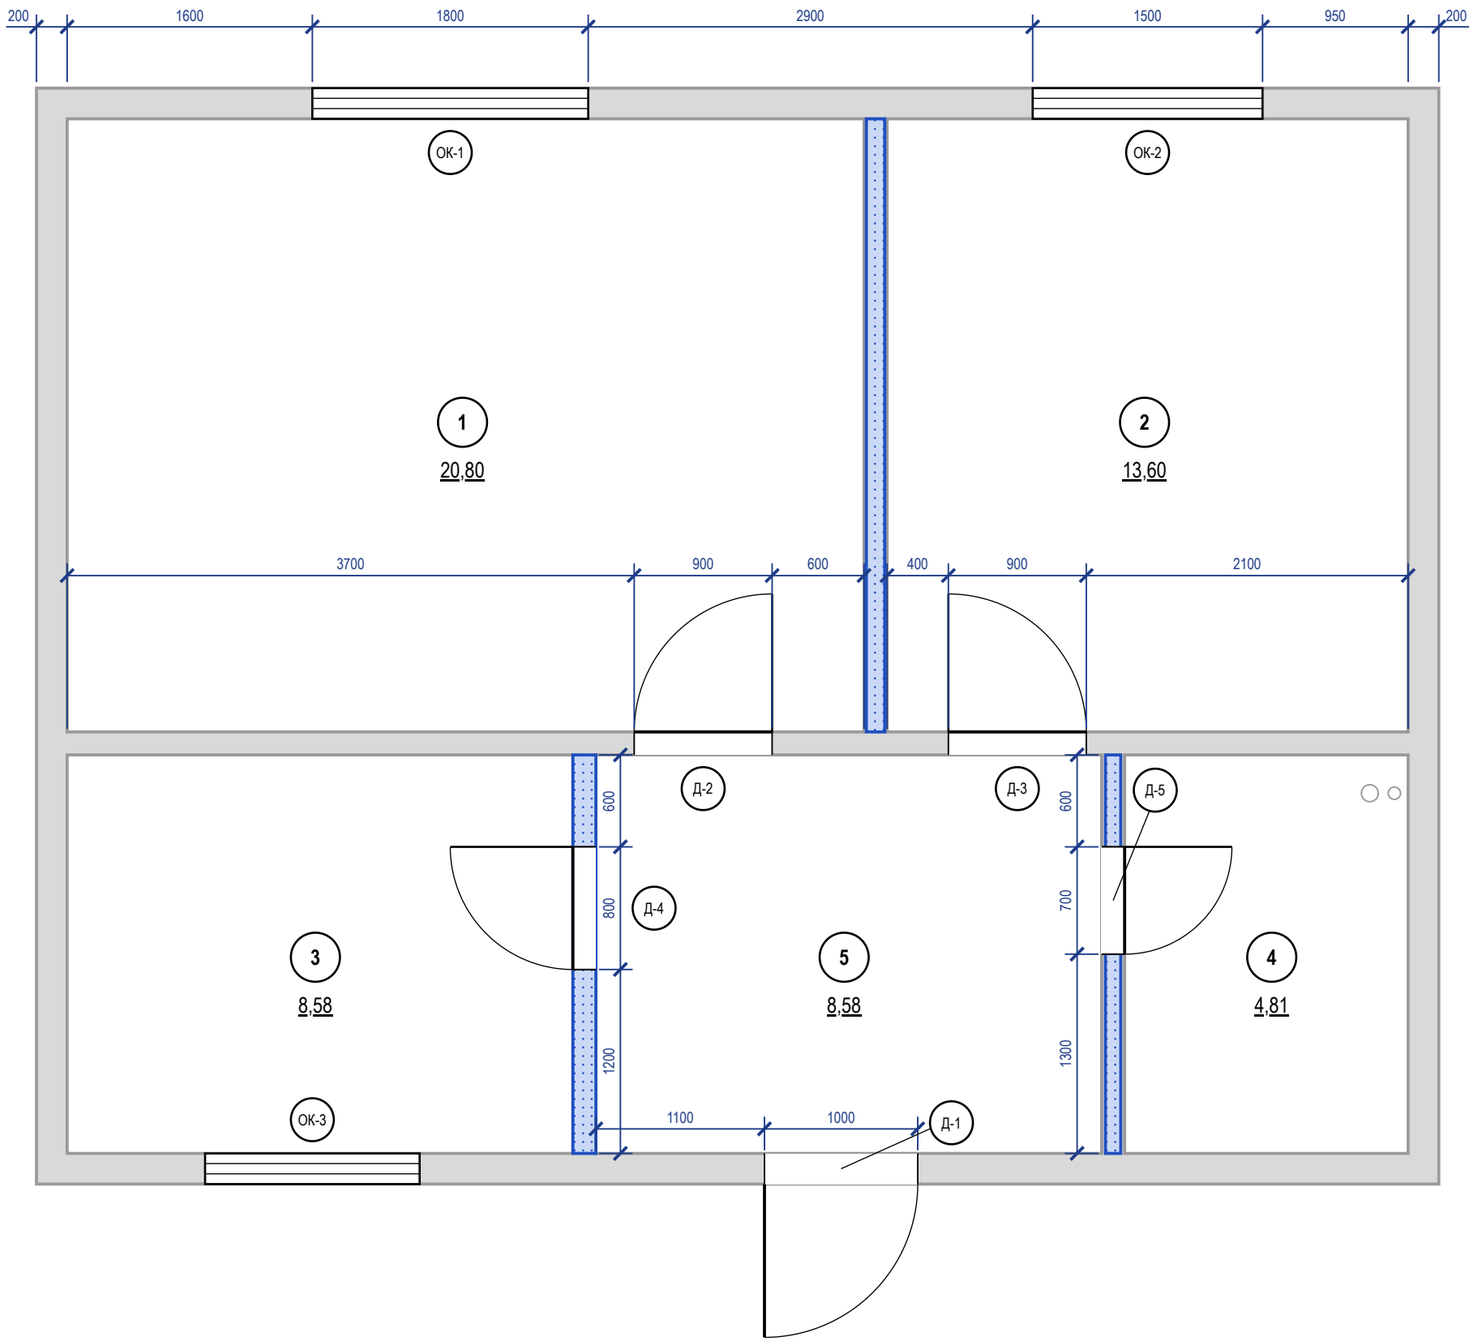

Примечания

1. Размеры проёмов и привязки — в миллиметрах от чистых граней стен до отделки; привязка — от угла того помещения, со стороны которого стоит размер. Размер проёма — ширина × высота от чистого пола 0,000. Размеры на плане — проёмов, не полотен: полотно — в ведомости, коробка — по системе. Откос от угла помещения до проёма с коробкой — не менее 50 мм.
2. Марки в кружках — типы заполнения проёмов (ГОСТ 21.501-2018, п. 5.3.2); одна марка — один типоразмер; количество сверено с планом.
3. Д-2, Д-3 — существующие проёмы, до техзаключения не расширять.
4. Экспликация помещений после перепланировки — лист 13; в марках помещений — номер и площадь, м².
5. Ведомость проёмов — лист 35: заполнение, открывание полотен, заказ и порядок монтажа блоков.

	Лист	№ док.	Подпись	Дата
Дизайнер	Кырлан А.С.			13.11.26
Проверил				
Н. контр.				
Утв.				

Проект: Квартира 56 м² — **М 1:40**

План размещения дверей

Стадия	Лист	Листов
П	34	92

выпуск 13.11.2026 № 568a382a0d · стр. 34 из 92


Ведомость заполнения проёмов

Марка	Наименование, обозначение	Проём ш×в, мм	Полотно (расч.)	Кол.	Откр.	Отделка полотна	Фурнитура	Прим.
Д-1	Блок дверной входной, ГОСТ 31173-2016	1000×2100	блок задать	1	Л	в комплекте блока	в комплекте блока (замки, глазок)	пом. 5; наружу
Д-2	Дверь скрытого монтажа, UNION FILO-60 Piatto	900×2100	800×2000	1	Л	окраска S 0804-Y30R с двух сторон	скрытые петли 3D, магнитный замок	
Д-3	Дверь скрытого монтажа, UNION FILO-60 Piatto	900×2100	800×2000	1	П	окраска S 0804-Y30R с двух сторон	скрытые петли 3D, магнитный замок	
Д-4	Дверь скрытого монтажа, UNION FILO-60 Piatto	800×2100	700×2000	1	Л	окраска S 0804-Y30R с двух сторон	скрытые петли 3D, магнитный замок	
Д-5	Дверь скрытого монтажа, UNION FILO-60 Piatto	700×2100	600×2000	1	П	в тон облицовки — пом. 4, S 0804-Y30R — пом. 5	скрытые петли 3D, магнитный замок, фиксатор WC	пом. 4; порог 15
ОК-1	Блок оконный, ГОСТ 23166-2021	1800×1500		1				пом. 1; низ 850
ОК-2	Блок оконный, ГОСТ 23166-2021	1500×1450		1				пом. 2; низ 900
ОК-3	Блок оконный, ГОСТ 23166-2021	1400×1450		1				пом. 3; низ 900


Примечания

1. Марки проёмов — те же, что на плане размещения дверей (лист 34); привязки проёмов — там же.
2. Открывание: Л — петли слева, П — справа, если смотреть со стороны, куда открывается полотно (на себя).
3. Скрытые двери (Д-2…Д-5): проём замерить в чистоте; блок заказать до штукатурки (≈ 30 дн.), короб ставить до штукатурки; полотно навесить после чистовой отделки, красить в цвет стен. Порядок — практика монтажа, изготовитель подтверждает.
4. Полотно «расч.» — по проёму и ряду изделия с запасом по каталогам, заказ — по таблице проёмов модели; Д-2…Д-5: проём 2100, а под полотно 2000 по каталогам нужен 2050–2080, под 2100 — 2150–2180: высоту проёма — по модели; Д-1: входной блок по ГОСТ 31173-2016 — задать при выборе блока.


Схемы дверных блоков (1:25) — вид со стороны открывания; вершина треугольника — сторона петель

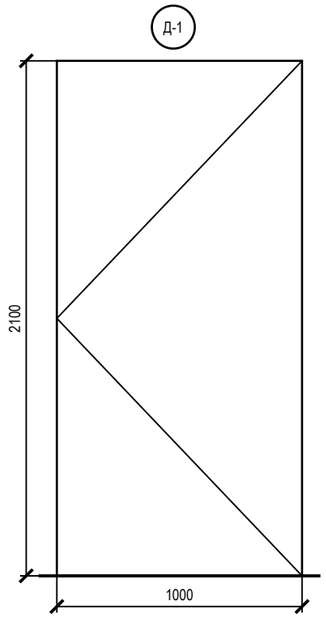


блок — по ГОСТ 31173
откр. Л

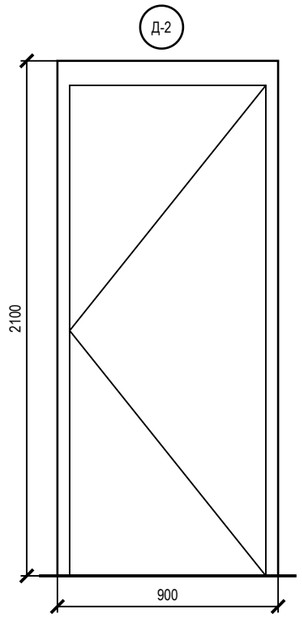


полотно 800×2000 (расч.)
откр. Л

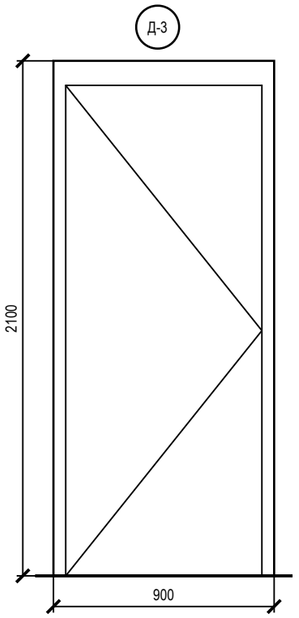

полотно 800×2000 (расч.)
откр. П

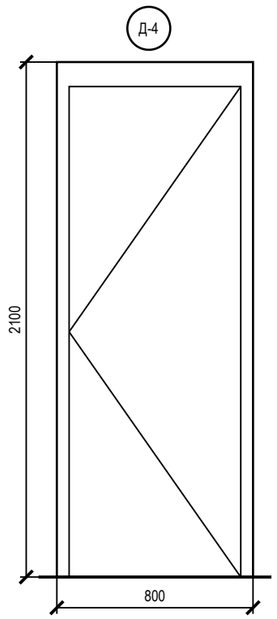


полотно 700×2000 (расч.)
откр. Л

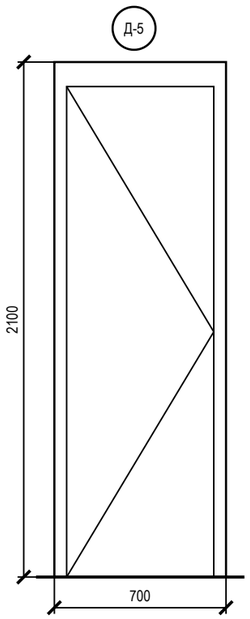

полотно 600×2000 (расч.)
откр. П

	Лист	№ док.	Подпись	Дата	Проект: Квартира 56 м²			
Дизайнер	Кырлан А.С.			13.11.26	Ведомость заполнения проёмов	Стадия	Лист	Листов
Проверил						П	35	92
Н. контр.								
Утв.								

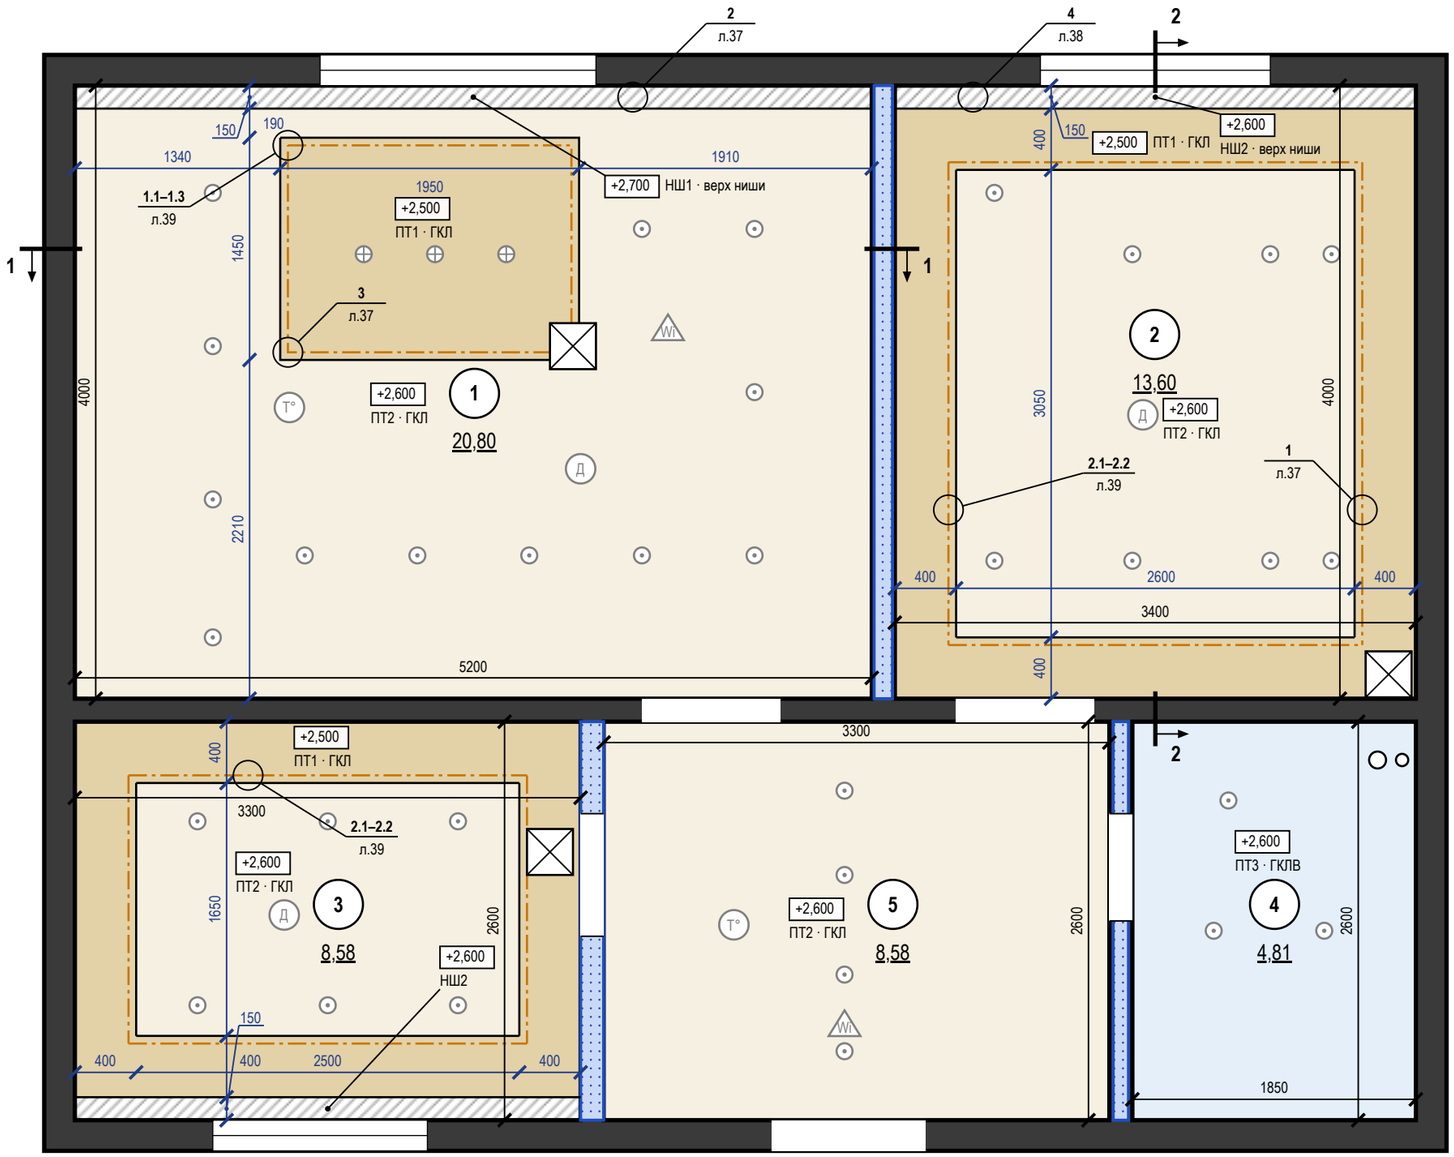

Ведомость потолков

Пом.	Марка	Конструкция	Низ / верх ниши	S, м²	Q
1	ПТ1	ГКЛ П113, остров + LED	+2,500	2,83	Q3
1	ПТ2	ГКЛ П113	+2,600	17,19	Q3
1	НШ1	ниша под шторы 150×100	+2,700	0,78	
2	ПТ1	ГКЛ П113, короб LED	+2,500	5,16	Q3
2	ПТ2	ГКЛ П113	+2,600	7,93	Q3
2	НШ2	ниша под шторы 150×100	+2,600	0,51	
3	ПТ1	ГКЛ П113, короб LED	+2,500	3,96	Q3
3	ПТ2	ГКЛ П113	+2,600	4,13	Q3
3	НШ2	ниша под шторы 150×100	+2,600	0,49	
4	ПТ3	ГКЛВ П113	+2,600	4,81	Q3
5	ПТ2	ГКЛ П113	+2,600	8,58	Q3
		Итого		**56,37**	

Ведомость вырезов и закладных в потолке

Марка	Устройство	Кол.	Пом.
	Светильник встраиваемый (марки — план освещения)	33	1, 2, 3, 4, 5
	Светильник подвесной (марки — план освещения)	3	1
ИП4, ИП1, ИП2	Извещатель дымовой	3	1, 2, 3
ИП5, ИП3	Извещатель тепловой	2	1, 5
АР2, АР1	Точка доступа Wi-Fi, PoE	2	1, 5
	Люк ревизии 300×300	3	1, 2, 3


Примечания

1. За отметку ±0,000 принят уровень чистого пола сухих помещений (готовое покрытие), а не существующего пола; пол пом. 4 — −0,015; верх плиты перекрытия −0,064 — расчётный по пирогу пола, не замерен; существующий пол снимается до плиты, его отметка не замерена. Отметки в прямоугольниках — низ потолка; низ плиты +2,700. Марка потолка — одна конструкция и отметка на весь альбом.
2. Потолки ГКЛ — каркасная система П113: подвесы через 1000 (с запасом: СП 163, табл. 14 — до 1100 при 0,15 кН/м²), несущие профили через 500, основные через 1200 мм; листы — поперёк несущих профилей. В помещениях 4 — ГКЛВ на оцинкованном каркасе.
3. Нижний уровень — пояс-короб по периметру шириной 400 мм, верхний — поле внутри пояса: пом. 2, 3.
4. LED-лента в алюминиевом профиле посередине карниза короба шириной 400 мм (узел 1, лист 37); длина по плану: пом. 2 — 11,7 м (в плане освещения 11,7); пом. 3 — 8,7 м (в плане освещения 8,7).
5. Ниши под шторы 150×100 мм — на всю длину стены с окном; карниз — на закладной до обшивки (узел 2 — пом. 1, лист 37; узел 4 — пом. 2, 3, лист 38).
6. Примыкание к стенам: теневой шов 15 мм, техзазор 3 мм — пом. 1, 2, 3, 5, по стенам, выровненным штукатуркой (узел 1); пом. 4 — разделительная лента.
7. Светильники и потолочные устройства — подложка с планов освещения, слаботочных систем и вентиляции (положение — по ним); вырезы и закладные — по ведомости на листе, до обшивки; отверстия не совмещать с профилями, глубина корпуса светильника до 70 мм.
8. Разрезы 1–1, 2–2 — на листе 37; высоты мебели и дверных блоков сверены с низом потолка в разрезах; гибка бортов фигур и ленты ниш — там же; размеры фигурных уровней — фрагмент 1 (лист 38).
9. Шпаклевание ГКЛ и условия приёмки — Q3: рассеянный дневной свет, осмотр с 2 м; боковой свет не оценивается.
10. Люки ревизии 300×300 мм — по центру блоков питания LED (БП4, БП1, БП2; координаты — план освещения).

	Лист	№ док.	Подпись	Дата	Проект: Квартира 56 м²			М 1:40
Дизайнер	Кырлан А.С.			13.11.26	План потолков	Стадия	Лист	Листов
Проверил						П	36	92
Н. контр.								
Утв.								


Разрез 1–1 (М 1:40)

Пом. 1 Гостиная-кухня; линия разреза — план потолков, лист 36

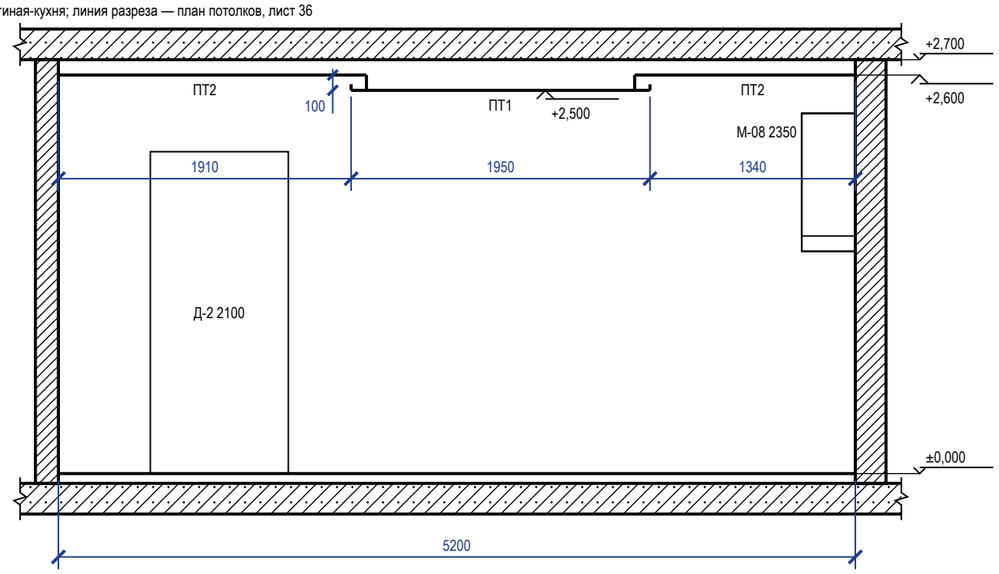


Разрез 2–2 (М 1:40)

Пом. 2 Спальня; линия разреза — план потолков, лист 36

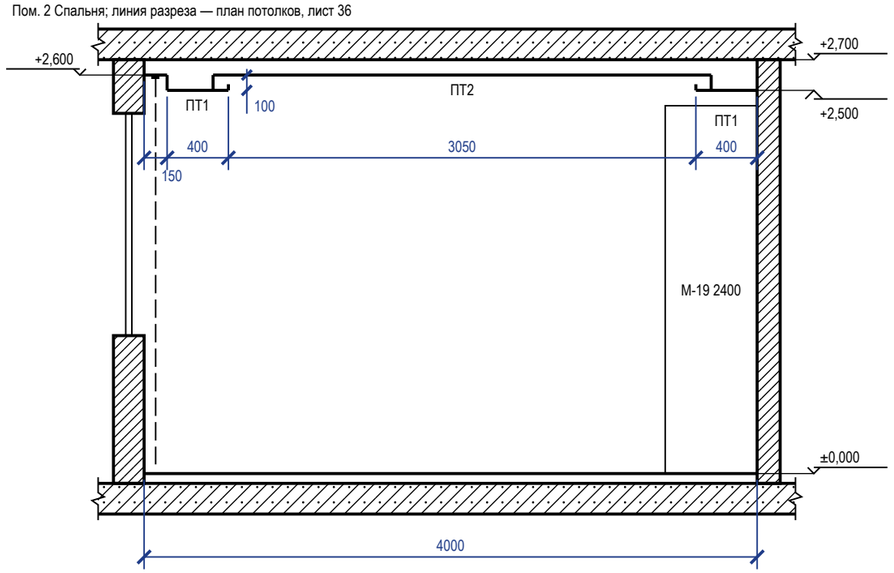

1 Короб с LED-подсветкой, теневой шов (М 1:10)


Пом. 2, 3; карниз 100×100, щель под свет 60 мм

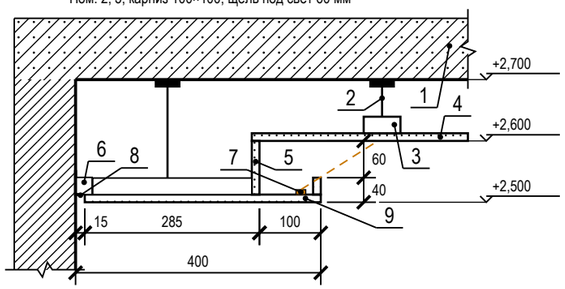

1 — плита перекрытия
2 — подвес прямой, шаг 1000 мм
3 — ПП 60×27: несущие через 500, основные через 1200 мм
4 — ГКЛ 12,5 по П113 — верхний уровень
5 — задняя стенка и бортик карниза — ГКЛ 12,5
6 — ПН 28×27 по периметру, к стене через 500 мм
7 — LED-лента в алюминиевом профиле
8 — теневой профиль: шов 15 мм, зазор 3 мм
9 — низ короба — ГКЛ 12,5 по ПП 60×27

2 Ниша под шторы (М 1:10)


Пом. 1; без подсветки; закладные под карниз — до обшивки

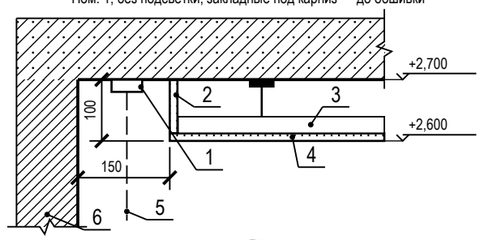

1 — карниз (шина), высота с верхом портьеры 80 мм
2 — стенка ниши — ГКЛ 12,5
3 — ПП 60×27 — каркас короба
4 — низ короба нижнего уровня — ГКЛ 12,5
5 — портьера
6 — стена с окном

3 Ниша LED фигурного уровня (М 1:10)

Пом. 1; карниз 100×100, щель под свет 60 мм

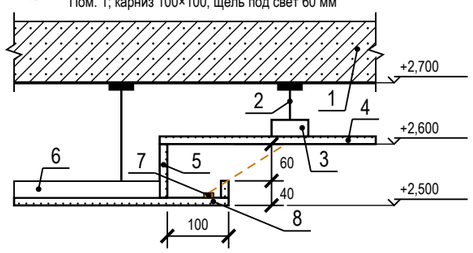

1 — плита перекрытия
2 — подвес прямой, шаг 1000 мм
3 — ПП 60×27: несущие через 500, основные через 1200 мм
4 — ГКЛ 12,5 по П113 — верхний уровень
5 — задняя стенка и бортик карниза — ГКЛ 12,5
6 — ПП 60×27 каркаса нижнего уровня, ПН по контуру фигуры (на дуге — с надрезами)
7 — LED-лента в алюминиевом профиле
8 — низ короба — ГКЛ 12,5 по ПП 60×27

Условные обозначения

- плита перекрытия в сечении
- стена в сечении
- потолок ГКЛ в сечении; под линией — марка потолка (план потолков)
- мебель и дверные проёмы за секущей плоскостью; число — марка и верх от чистого пола, мм
- портьера в нише под шторы


Примечания

1. Разрезы — по линиям 1–1, 2–2 на плане потолков (лист 36). Отметки — от ±0,000 чистого пола, м; размеры — мм.
2. Высоты мебели и дверных блоков за секущей плоскостью сверены с низом потолка над ними: верх ниже низа короба и поля.
3. ГКЛ 12,5 мм по каркасу П113; перепад уровней и бортик карниза — ГКЛ по ПП 60×27 (узел 1 — на этом листе). Ниша под шторы — на всю длину стены с окном, карниз на закладной до обшивки (узел 2 — на этом листе; узел 4 — лист 38).
4. Толщины плит перекрытия и пирога пола показаны условно.
5. Сечения потолков по помещениям М 1:10 (отметки помещения, профили, подвесы, крепёж, изделия) — лист 39.
6. Ведомость объёмов потолков (лист ГКЛ, профиль, подвесы, лента, блоки питания, люки) — на листе 38.
7. Фрагмент 1 — помещение с фигурными уровнями (размеры фигур, радиусы, отметки) — на листе 38.

	Лист	№ док.	Подпись	Дата	Проект: Квартира 56 м²			М 1:40; 1:10
Дизайнер	Кырлан А.С.			13.11.26	Разрезы и узлы потолков	Стадия	Лист	Листов
Проверил						П	37	92
Н. контр.								
Утв.								

Фрагмент 1. Пом. 1 Гостиная-кухня — уровни потолка (М 1:50)

Цепочки — от чистых граней стен; отметки — низ уровня от ±0,000

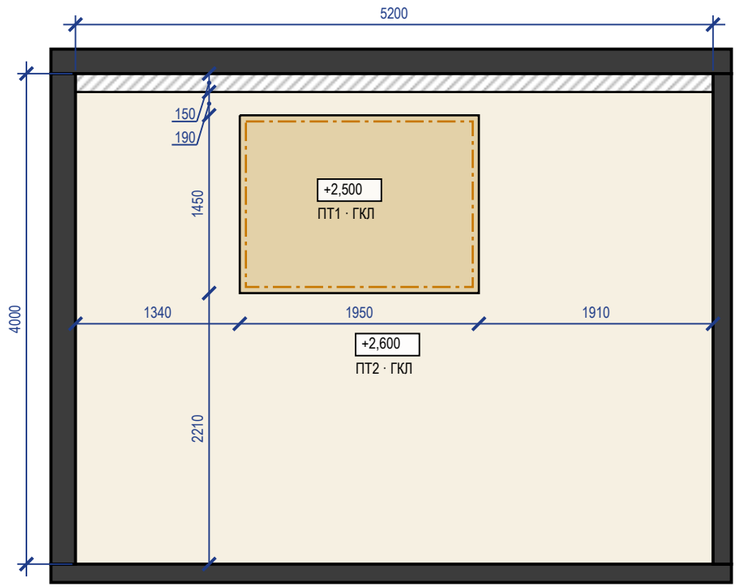

ПТ1 — низ +2,500

ПТ2 — низ +2,600

LED-лента в нише подсветки (карниз короба, ниша фигуры)


ниша под шторы

Ведомость объёмов потолков

Позиция	Ед.	Кол.	Пом.
Лист ГКЛ 12,5	м²	59,20	1, 2, 3, 5
Лист ГКЛВ 12,5	м²	4,81	4
Борта и карнизы (входят в площади листов выше)	м²	7,64	1, 2, 3
Профиль ПП 60×27	м	169,21	1, 2, 3, 4, 5
Профиль ПН 28×27	м	169,50	1, 2, 3, 4, 5
Подвес прямой	шт.	72	1, 2, 3, 4, 5
Анкер-клин к плите	шт.	72	1, 2, 3, 4, 5
Шуруп TN 3,5×25	шт.	1472	1, 2, 3, 4, 5
Лента армирующая для швов	м	76,81	1, 2, 3, 4, 5
Шпаклёвка для швов	кг	25,60	1, 2, 3, 4, 5
Грунтовка (швы)	л	6,40	1, 2, 3, 4, 5
Лента разделительная по периметру	м	65,70	1, 2, 3, 4, 5
Сплошная шпаклёвка и окраска (площадь развёртки)	м²	64,01	1, 2, 3, 4, 5
Лента LED	м	26,80	1, 2, 3
Требуемая мощность блоков питания	Вт	334	1, 2, 3
Установленная мощность блоков питания	Вт	700	1, 2, 3
Блок питания LED	шт.	3	1, 2, 3
Люк ревизии	шт.	3	1, 2, 3

4 Ниша под шторы (М 1:10)

Пом. 2, 3; без подсветки; закладные под карниз — до обшивки

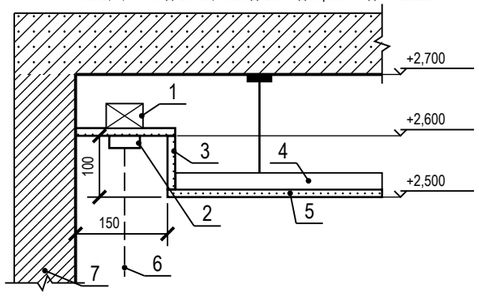

1 — закладная под карниз — брус 40×50

2 — карниз (шина), высота с верхом портьеры 80 мм

3 — стенка и потолок ниши — ГКЛ 12,5

4 — ПП 60×27 — каркас короба

5 — низ короба нижнего уровня — ГКЛ 12,5

6 — портьера

7 — стена с окном

Примечания


1. ГКЛ 12,5 мм по каркасу П113; узлы коробов и ниш под шторы: узел 1 — лист 37; узел 2 — лист 37; узел 4 — на этом листе; условные обозначения разрезов — на листе 37.
2. Фрагмент 1 (план потолков — лист 36) — фигурные уровни потолка крупно: привязки краёв и центров фигур к чистым граням стен, радиусы (R) с центрами, хорда и стрелка дуги, отметки низа каждого уровня; цвета уровней — как на плане потолков.
3. Фигурные уровни: борт — ГКЛ по ПН с надрезами (на дуге шаг стоек борта 300 мм при R до 2500, 400 — до 5000) или по гнутому заводскому профилю (СП 163, 6.3.3). Лента в нише фигуры по оси: остров пом. 1 — 6,4 м; узел ниши LED фигуры: узел 3 — лист 37 — пом. 1.
4. Ведомость объёмов — по геометрии плана потолков: Лист ГКЛ 12,5 — плоскости уровней + борта (без арочных участков); Лист ГКЛВ 12,5 — плоскости уровней + борта; Борта и карнизы — длина перепада × перепад; Профиль ПП 60×27 — S × (1/шаг несущ. + 1/шаг осн.) + стойки бортов; Профиль ПН 28×27 — периметр стен + 2 × перепады + карнизы; Подвес прямой — по раскладке: S уровня / (шаг осн. × шаг подвесов), пояс уже шага — ряд вдоль пояса, фигура — по контуру; шаг подвесов — не больше табл. 14 СП 163; Анкер-клин к плите — по одному на подвес (Knauf П113); Шуруп TN 3,5×25 — 23 шт./м² (Knauf П113, табл. 2 альбома П 11); Лента армирующая для швов — 1,2 м/м² листа (Knauf); Шпаклёвка для швов — 0,4 кг/м² листа, только швы (Knauf); Грунтовка (швы) — 0,1 л/м² листа, только швы (Knauf); Лента разделительная по периметру — периметр стен под потолком ГКЛ; Сплошная шпаклёвка и окраска (площадь развёртки) — плоскости + борта; расход — по паспорту материала (норма расхода на сплошной слой не подтверждена); Лента LED — по оси карниза и ниши фигуры (план потолков); Требуемая мощность блоков питания — Вт/м × длина × 1,3; Установленная мощность блоков питания — сумма мощностей блоков по плану освещения; Блок питания LED — блоки потолочных лент по плану освещения (БП4, БП1, БП2); Люк ревизии — план потолков; без запаса на подрезку (при закупке листа: ×1,075 при S > 20 м², ×1,175 — 10–20 м², ×1,275 — < 10 м²).

	Лист	№ док.	Подпись	Дата	Проект: Квартира 56 м²	М 1:50; 1:10		
Дизайнер	Кырлан А.С.			13.11.26	Разрезы и узлы потолков (продолжение)	Стадия	Лист	Листов
Проверил						П	38	92
Н. контр.								
Утв.								

выпуск 13.11.2026 № 568a382a0d · стр. 38 из 92

Сечение 1.1. Ниша LED фигурного уровня (М 1:10)


Пом. 1 Гостиная-кухня; карниз 100×100, щель под свет 60 мм

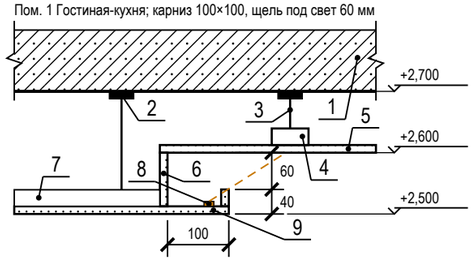

1 — плита перекрытия
2 — анкер-клин к плите — по одному на подвес
3 — подвес прямой, шаг 1000 мм
4 — ПП 60×27: несущие через 500, основные через 1200 мм; соединители одноуровневые, шурупы LN 3,5×9
5 — ГКЛ 12,5 по П113 — верхний уровень; шурупы TN 3,5×25 через 170 мм
6 — задняя стенка и бортик карниза — ГКЛ 12,5
7 — ПП 60×27 каркаса нижнего уровня, ПН по контуру фигуры (на дуге — с надрезами)
8 — LED-лента 9,6 Вт/м, 24 В в алюминиевом профиле
9 — низ короба — ГКЛ 12,5 по ПП 60×27

Сечение 1.2. Ниша под шторы (М 1:10)


Пом. 1 Гостиная-кухня; без подсветки; закладные под карниз — до обшивки

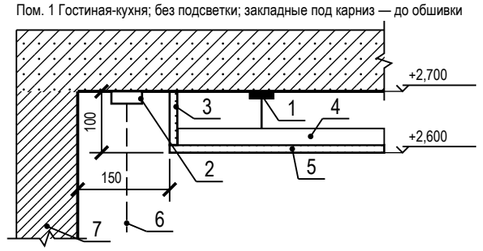

1 — анкер-клин к плите — по одному на подвес; подвес прямой, шаг 1000 мм
2 — карниз (шина), высота с верхом портьеры 80 мм
3 — стенка ниши — ГКЛ 12,5
4 — ПП 60×27 — каркас короба, основные через 1200 мм; соединители одноуровневые, шурупы LN 3,5×9
5 — низ короба нижнего уровня — ГКЛ 12,5; шурупы TN 3,5×25 через 170 мм
6 — портьера
7 — стена с окном

Сечение 1.3. Примыкание потолка к стене (М 1:10)


Пом. 1 Гостиная-кухня; примыкание — теневой шов

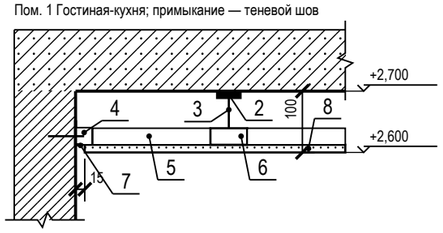

1 — плита перекрытия
2 — анкер-клин к плите — по одному на подвес
3 — подвес прямой, шаг 1000 мм
4 — ПН 28×27 по периметру — дюбель-гвоздь через ≤ 500 мм, не менее 3 на профиль
5 — ПП 60×27 несущий (вид) через 500 мм, в ПН
6 — ПП 60×27 основной (сечение) через 1200 мм; соединители одноуровневые, шурупы LN 3,5×9
7 — теневой профиль: шов 15 мм, зазор 3 мм; стена под шов выровнена
8 — ГКЛ 12,5 по П113; шурупы TN 3,5×25 через 170 мм

Сечение 2.1. Короб с LED-подсветкой, теневой шов (М 1:10)


Пом. 2 Спальня, 3 Детская; карниз 100×100, щель под свет 60 мм

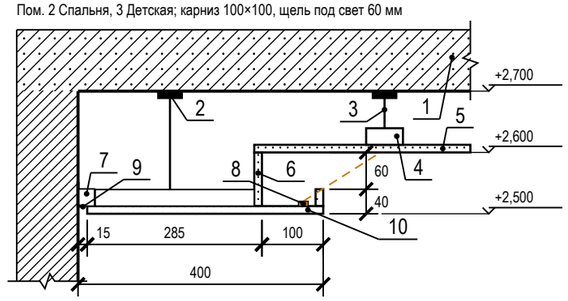

1 — плита перекрытия
2 — анкер-клин к плите — по одному на подвес
3 — подвес прямой, шаг 1000 мм
4 — ПП 60×27: несущие через 500, основные через 1200 мм; соединители одноуровневые, шурупы LN 3,5×9
5 — ГКЛ 12,5 по П113 — верхний уровень; шурупы TN 3,5×25 через 170 мм
6 — задняя стенка и бортик карниза — ГКЛ 12,5
7 — ПН 28×27 по периметру — дюбель-гвоздь через ≤ 500 мм, не менее 3 на профиль
8 — LED-лента 9,6 Вт/м, 24 В в алюминиевом профиле
9 — теневой профиль: шов 15 мм, зазор 3 мм
10 — низ короба — ГКЛ 12,5 по ПП 60×27

Сечение 2.2. Ниша под шторы (М 1:10)

Пом. 2 Спальня, 3 Детская; без подсветки; закладные под карниз — до обшивки

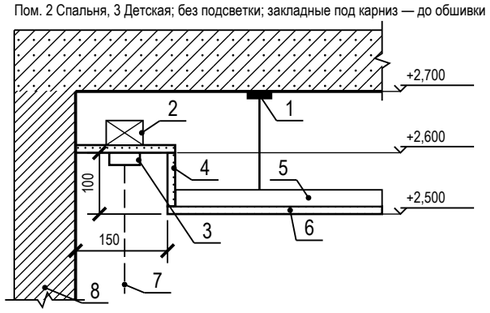

1 — анкер-клин к плите — по одному на подвес; подвес прямой, шаг 1000 мм
2 — закладная под карниз — брус 40×50
3 — карниз (шина), высота с верхом портьеры 80 мм
4 — стенка и потолок ниши — ГКЛ 12,5
5 — ПП 60×27 — каркас короба, основные через 1200 мм; соединители одноуровневые, шурупы LN 3,5×9
6 — низ короба нижнего уровня — ГКЛ 12,5; шурупы TN 3,5×25 через 170 мм
7 — портьера
8 — стена с окном

Условные обозначения


— · — LED-лента в нише подсветки (карниз короба, ниша фигуры)

Примечания

1. Сечения потолков М 1:10 по помещениям с нишами LED и нишами под шторы: отметки и размеры этого помещения от ±0,000 чистого пола (м, мм). Положение — по плану потолков (лист 36): короб и ниша LED — по линиям ленты, ниша под шторы — у стены с окном; типовые узлы по группам помещений — на листе 37.
2. Крепёж: подвес прямой к плите на анкер-клине — по одному на подвес (Knauf П113); ПН к стенам — дюбель-гвоздь через ≤ 500 мм, не менее 3 на профиль (серия 1.045.9-2.08); лист 12,5 — шурупы TN 3,5×25 через 170 мм (СП 163, табл. 15); профили между собой — соединители одноуровневые, шурупы LN 3,5×9.
3. Изделие карниза, профиля LED и галтели подписано артикулом из данных; где артикул не выбран, сечение дано по габаритам из данных (ширина и глубина ниши, щель под свет), изделие подбирается по ним.

	Лист	№ док.	Подпись	Дата	Проект: Квартира 56 м²		М 1:10	
Дизайнер	Кырлан А.С.			13.11.26	Сечения потолков М 1:10	Стадия	Лист	Листов
Проверил						П	39	92
Н. контр.								
Утв.								

выпуск 13.11.2026 № 568a382a0d · стр. 39 из 92

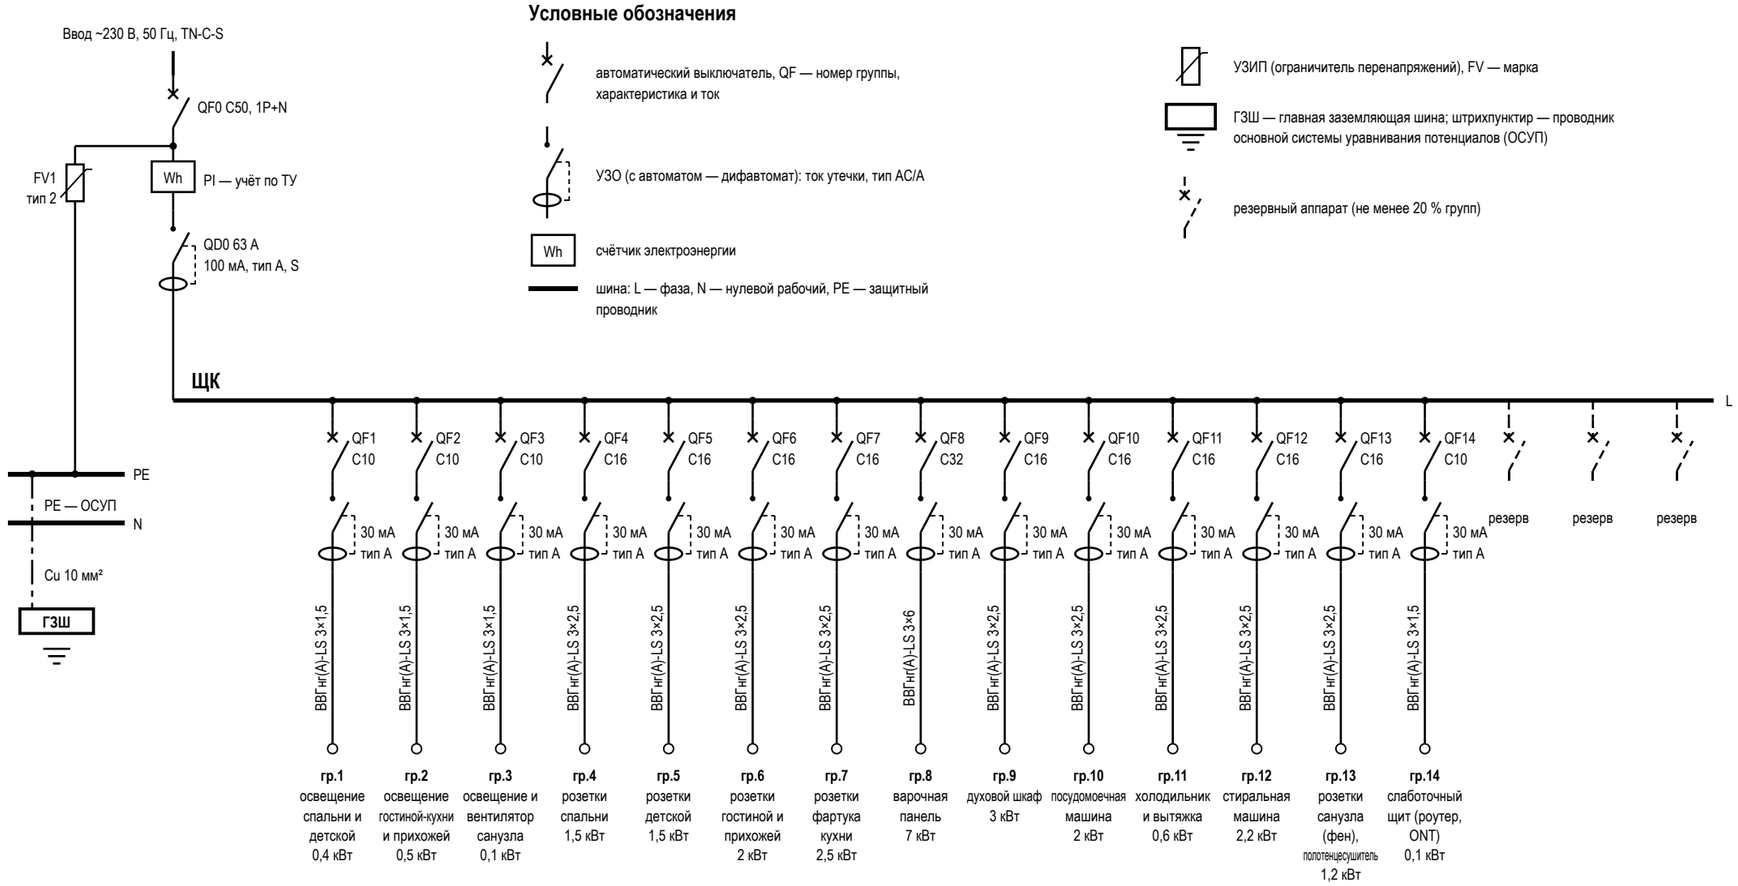

Условные обозначения

автоматический выключатель, QF — номер группы, характеристика и ток

УЗО (с автоматом — дифавтомат): ток утечки, тип AC/A

Wh — счётчик электроэнергии

шина: L — фаза, N — нулевой рабочий, PE — защитный проводник

УЗИП (ограничитель перенапряжений), FV — марка

ГЗШ — главная заземляющая шина; штрихпунктир — проводник основной системы уравнивания потенциалов (ОСУП)

резервный аппарат (не менее 20 % групп)

Данные щитка

Показатель	Значение
Номер щитка	ЩК
Тип	ЩРВ-П-48, IP41
Уст. мощность, кВт	24,6
Разреш. мощность, кВт	10
Расчётная, кВт	9,6
Автоматы 1п: занят. / рез.	14 / 3
Модулей: всего / занято	48 / 34
Ток на вводе, А	50
Вводной аппарат	QF0 C50, 1P+N
УЗИП	FV1, тип 2, ЩК, после счётчика
ГЗШ, проводник ОСУП	Cu 10 мм²

Таблица групп щита ЩК и кабельный журнал

№	Назначение	Помещения	Автомат	УЗО / дифавтомат	Кабель	Длина, м	Р, кВт	Точек
1	освещение спальни и детской	2, 3	C10	30 мА, тип A	ВВГнг(A)-LS 3×1,5	70,6	0,4	27
2	освещение гостиной-кухни и прихожей	1, 5	C10	30 мА, тип A	ВВГнг(A)-LS 3×1,5	71,9	0,5	32
3	освещение и вентилятор санузла	4, 5	C10	30 мА, тип A	ВВГнг(A)-LS 3×1,5	15,7	0,1	6
4	розетки спальни	2	C16	30 мА, тип A	ВВГнг(A)-LS 3×2,5	24,9	1,5	6
5	розетки детской	3	C16	30 мА, тип A	ВВГнг(A)-LS 3×2,5	20,5	1,5	4
6	розетки гостиной и прихожей	1, 5	C16	30 мА, тип A	ВВГнг(A)-LS 3×2,5	43,2	2	9
7	розетки фартука кухни	1	C16	30 мА, тип A	ВВГнг(A)-LS 3×2,5	29,6	2,5	6
8	варочная панель	1	C32	30 мА, тип A	ВВГнг(A)-LS 3×6	16,5	7	1
9	духовой шкаф	1	C16	30 мА, тип A	ВВГнг(A)-LS 3×2,5	16,5	3	1
10	посудомоечная машина	1	C16	30 мА, тип A	ВВГнг(A)-LS 3×2,5	14	2	1
11	холодильник и вытяжка	1	C16	30 мА, тип A	ВВГнг(A)-LS 3×2,5	16,3	0,6	2
12	стиральная машина	4	C16	30 мА, тип A	ВВГнг(A)-LS 3×2,5	7,5	2,2	1
13	розетки санузла (фен), полотенцесушитель	4	C16	30 мА, тип A	ВВГнг(A)-LS 3×2,5	13,6	1,2	2
14	слаботочный щит (роутер, ONT)	5	C10	30 мА, тип A	ВВГнг(A)-LS 3×1,5	5,4	0,1	1
	Итого по сечениям ВВГнг(A)-LS, м: 3×1,5 — 163,6; 3×2,5 — 186,1; 3×6 — 16,5					366,2		

Примечания

1. Схема однолинейная: одна линия — фаза, N и PE группы; аппараты — в отключённом положении (ГОСТ 2.702, ГОСТ 2.755). Номера групп — как у точек на планах (гр.). За отметку 0,000 принят уровень чистого пола; высота щита — по плану розеток.
2. Розеточные и мокрые линии — через УЗО или дифавтомат с током утечки не более 30 мА (ПУЭ 7.1.79); в санузле выполнить ДСУП (ПУЭ 7.1.87–7.1.88).
3. УЗО тип A — для линий с электроникой, стиральной и посудомоечной машиной, LED-драйверами; тип AC — только для чисто активной нагрузки.
4. Кабель — медный, исполнение нг(A)-LS (ГОСТ 31565-2012); скрытая прокладка только горизонтально и вертикально, фактические трассы зафиксировать исполнительной схемой до закрытия отделкой.
5. Номинал автомата — не выше допустимого тока кабеля: 1,5 мм² — до 10 А, 2,5 мм² — до 16 А. Резерв щита — не менее 20 % модулей.
6. Расчёт нагрузок, токов КЗ, селективности и сечений — по проекту ЭОМ организации с допуском СРО; лист задаёт состав, расположение и группы.
7. УЗИП FV1 — после вводного автомата, проводник к шине PE — кратчайший, без петель. Шина PE щита соединяется с ГЗШ проводником ОСУП; к ГЗШ присоединяются трубы водопровода и отопления на вводе в квартиру (ПУЭ 7.1.87). Шины N и PE — раздельные, после разделения PEN не объединяются.
8. До подключения нагрузки — приёмо-сдаточные испытания с протоколом: сопротивление изоляции линий не менее 0,5 МОм, срабатывание УЗО по току и времени, непрерывность защитных проводников PE (ПУЭ, гл. 1.8).

	Лист	№ док.	Подпись	Дата	Проект: Квартира 56 м²			
Дизайнер	Кырлан А.С.			13.11.26	Однолинейная схема щита	Стадия	Лист	Листов
Проверил						П	40	92
Н. контр.								
Утв.								

Группы щита ЩК (1)

№	Назначение	Руст, кВт	Кс	Ррасч, кВт	Iрасч, А	Автомат	Кабель
1	освещение спальни и детской	0,4	0,6	0,24	1,1	C10	3×1,5
2	освещение гостиной-кухни и прихожей	0,5	0,6	0,3	1,4	C10	3×1,5
3	освещение и вентилятор санузла	0,1	0,6	0,06	0,3	C10	3×1,5
4	розетки спальни	1,5	0,4	0,6	2,7	C16	3×2,5
5	розетки детской	1,5	0,4	0,6	2,7	C16	3×2,5
6	розетки гостиной и прихожей	2	0,4	0,8	3,7	C16	3×2,5
7	розетки фартука кухни	2,5	0,4	1	4,6	C16	3×2,5

Группы щита ЩК (2)

№	Назначение	Руст, кВт	Кс	Ррасч, кВт	Iрасч, А	Автомат	Кабель
8	варочная панель	7	0,6	4,2	19,2	C32	3×6
9	духовой шкаф	3	0,6	1,8	8,2	C16	3×2,5
10	посудомоечная машина	2	0,7	1,4	6,4	C16	3×2,5
11	холодильник и вытяжка	0,6	0,4	0,24	1,1	C16	3×2,5
12	стиральная машина	2,2	0,7	1,54	7	C16	3×2,5
13	розетки санузла (фен), полотенцесушитель	1,2	0,7	0,84	3,8	C16	3×2,5
14	слаботочный щит (роутер, ONT)	0,1	0,4	0,04	0,2	C10	3×1,5

Итог по квартире

Показатель	Значение
Установленная мощность Σ Руст	24,6 кВт
Σ Руст × Кс по группам	13,66 кВт
Коэффициент одновременности	0,7
Расчётная мощность квартиры Ррасч	9,6 кВт
Расчётный ток Iрасч (230 В, cosφ 0,95)	44 А
Разрешённая мощность	10 кВт
Запас до разрешённой	4,4 % — меньше 10 %
Вводной аппарат	C50, 1P+N


Примечания

1. Руст — установленная мощность группы по данным щита (приборы — по паспорту, розетки общего назначения — оценка 0,1 кВт на гнездо). Кс — коэффициенты спроса: освещение 0,6; розетки 0,4; варочная и духовой 0,6; кондиционеры 0,8; тёплый пол 1,0; прочие 0,7; одновременность 0,7.
2. Коэффициенты — ориентир исполнителя, не табличные значения нормы; расчёт нагрузки подтверждает инженер ЭОМ (СП 256.1325800.2016). Под разрешённую мощность они не подгоняются.
3. Вывод: запас 4,4 % < 10 % (расчётная 9,6 кВт при разрешённой 10 кВт). Это вопрос заказчику (реестр K-N): запросить увеличение мощности у сетевой организации либо принять приоритетное отключение нагрузок (тёплый пол, кондиционеры, вторая машина) при работе плиты.
4. Розеточные и мокрые линии — через УЗО или дифавтомат с током утечки не более 30 мА (ПУЭ 7.1.79); в санузле выполнить ДСУП (ПУЭ 7.1.87–7.1.88).

	Лист	№ док.	Подпись	Дата	Проект: Квартира 56 м²			
Дизайнер	Кырлан А.С.			13.11.26				
Проверил					Таблица нагрузок щита	Стадия	Лист	Листов
Н. контр.								
Утв.						П	41	92

выпуск 13.11.2026 № 568a382a0d · стр. 41 из 92

План принципиальных трасс (М 1:50)

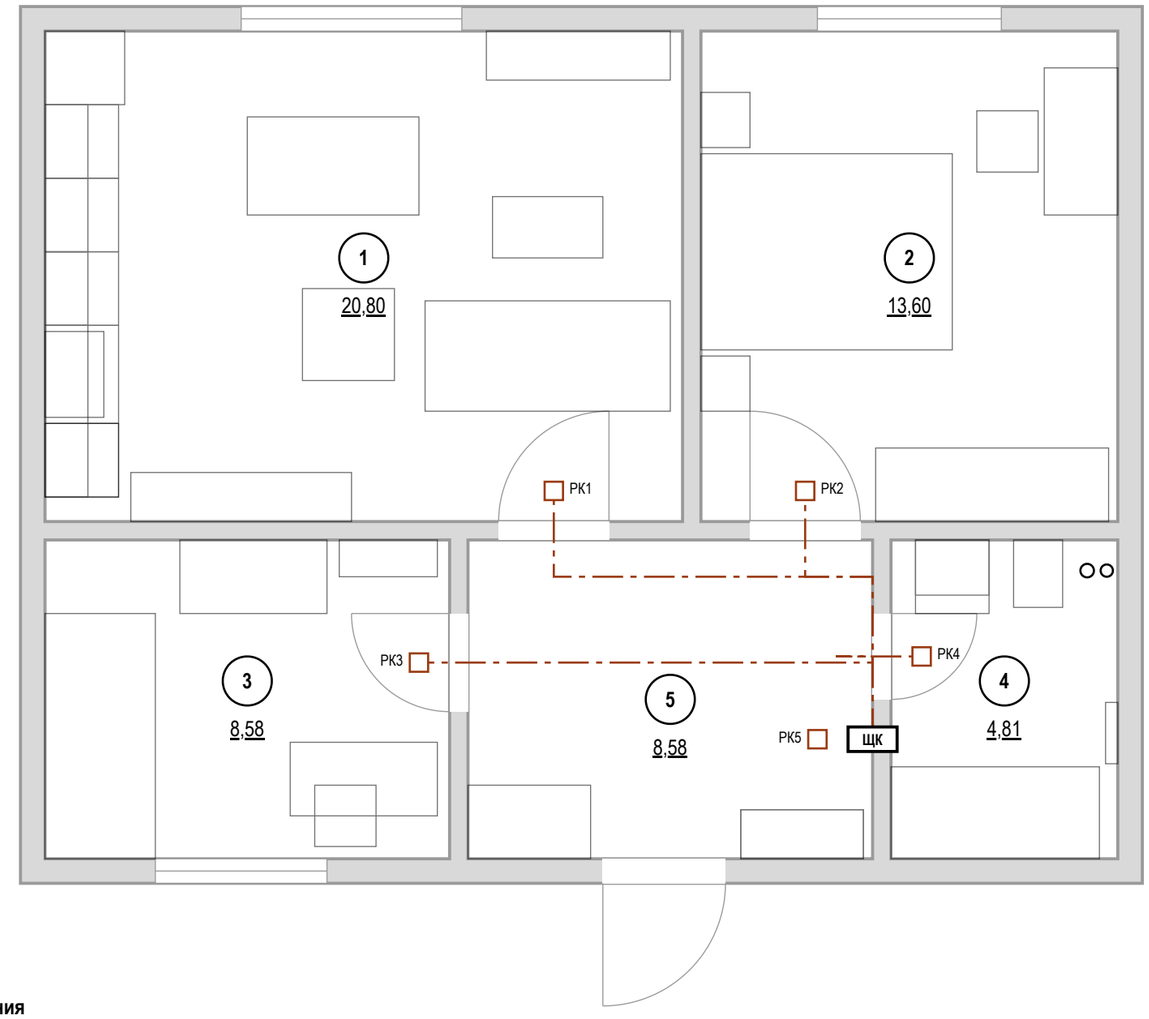

Кабель по группам ВВГнг(А)-LS, м

Гр.	мм²	Трасса	Данные
1	3×1,5	70,6	70,6
2	3×1,5	72,8	71,9
3	3×1,5	15,8	15,7
4	3×2,5	24,9	24,9
5	3×2,5	20,5	20,5
6	3×2,5	43,2	43,2
7	3×2,5	30,5	29,6

Гр.	мм²	Трасса	Данные
8	3×6	16,5	16,5
9	3×2,5	16,5	16,5
10	3×2,5	14	14
11	3×2,5	16,3	16,3
12	3×2,5	7,4	7,5
13	3×2,5	13,7	13,6
14	3×1,5	5,4	5,4
Σ		**368,1**	**366,2**

Экспликация помещений

№	Помещение	Площадь, м²
1	Гостиная-кухня	20,80
2	Спальня	13,60
3	Детская	8,58
4	Санузел	4,81
5	Прихожая	8,58
	Итого (общая площадь)	56,37

Объёмы прокладки

Работа, материал	Ед.	Кол.
Гофротруба Ø20 в потолочном пространстве	м	129,5
Кабель-канал плинтуса для силовых линий	м	95,3
Короб или накладной канал для вертикальных спусков и подъёмов	м	73,4
Коробка распределительная (РК) над дверью помещения	шт	5
Слаботочка: кабель домофона	м	6,7
Слаботочка: Кабель коаксиальный RG-6 (75 Ом) к розеткам ТВ	м	11,7
Слаботочка: U/UTP кат. 6 (LAN, Wi-Fi, камеры)	м	44,9
Слаботочка: гофротруба Ø20 отдельно от силовых	м	57

Штробы — только после заключения

Работа	Ед.	Кол.
Вертикальные штробы 20×20 мм от потолка до каждой настенной точки (в маршрут без штроб не входят)	м	91,05

Условные обозначения


- **ЩК** — щит квартирный
- РК — распределительная коробка над дверью помещения
- магистраль от щита к РК: потолочное пространство, гофра
- мебель и сантехприборы — подложка

Примечания

1. За отметку 0,000 принят уровень чистого пола. Высоты Н — от чистого пола до оси изделия; привязки — от чистовой грани стены до оси механизма (у рамки на несколько постов — до оси рамки).
2. Розеточные и мокрые линии — через УЗО или дифавтомат с током утечки не более 30 мА (ПУЭ 7.1.79); в санузле выполнить ДСУП (ПУЭ 7.1.87–7.1.88).
3. Кабель — медный, исполнение нг(А)-LS (ГОСТ 31565-2012); скрытая прокладка только горизонтально и вертикально, фактические трассы зафиксировать исполнительной схемой до закрытия отделкой.
4. Расчёт нагрузок, токов КЗ, селективности и сечений — по проекту ЭОМ организации с допуском СРО; лист задаёт состав, расположение и группы.
5. Длины — по плану: от щита вверх в потолочное пространство, по дверям и коридору без захода в мокрые помещения к распределительной коробке над дверью, далее к точкам; вертикали считаются вниз и обратно (у последней точки цепочки — в один конец); запас 10 %. Трассы принципиальные: фактическую зафиксировать исполнительной схемой до закрытия отделкой.
6. Несущие стены не определены: штробы в стенах не выполнять. Маршрут проложен без штроб: горизонтали — за потолком в гофре (129,5 м) и в кабель-канале плинтуса (95,3 м), вертикали — в коробе или накладном канале (129,2 м кабеля). Точек: за потолком — 43, спуск из потолка — 12, по плинтусу — 14, плинтус и подъём 30.
7. Вариант со штробами — работа после технического заключения: 91,05 м вертикальных штроб от потолка до каждой настенной точки; условие — только после технического заключения: стена не несущая (или вертикальная штроба в несущей согласована конструктором), глубина и ширина 20–25 мм, не в зонах 0–2 ванной. Без заключения и согласования конструктора в смету и в график эта работа не входит.
8. В данных проекта (журнал щита) длины кабеля внесены оценкой (366 м), по трассам из геометрии — 368 м (+1 %): к закупке и в смету принимать длины по трассам, а оценку в данных проекта заменить.
9. Слаботочные сети: кабели и точки считаются по лучам от ЩС (лист слаботочных сетей): 63 м, портов патч-панели и коммутатора не менее 5; из точек 2 предложения листа слаботочки, не подтверждённые заказчиком. Изделия — в ведомости изделий.

	Лист	№ док.	Подпись	Дата	Проект: Квартира 56 м²			М 1:50
Дизайнер	Кырлан А.С.			13.11.26	План принципиальных трасс	Стадия	Лист	Листов
Проверил						П	42	92
Н. контр.								
Утв.								

План розеток (М 1:40)

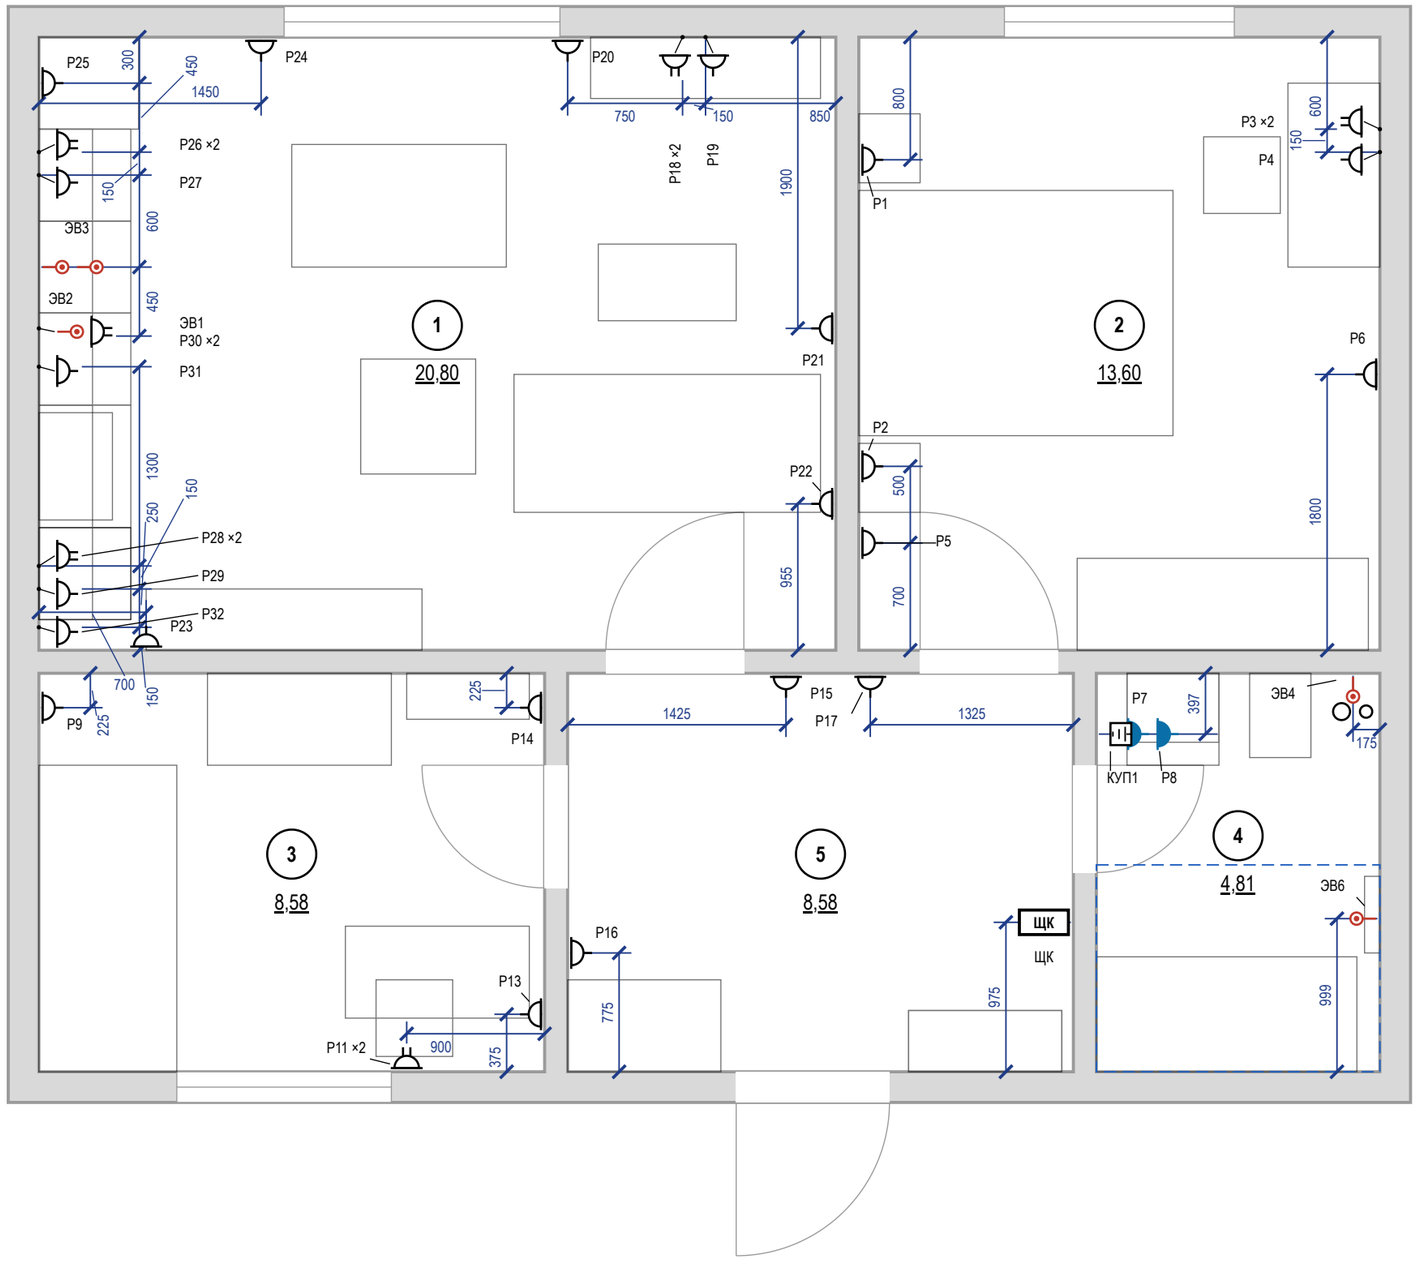

Условные обозначения

Знак	Тип изделия	Н, мм	Кол., шт
	Розетка с заземлением	300	12
	То же	у знака	10
	Блок розеток с заземлением, рамка 2 поста	300	1
	То же	у знака	5
	Розетка с заземлением IP44	у знака	2
	Вывод кабеля к прибору	у знака	5
	КУП (уравнивание потенциалов)	300	1
ЩК	Щит квартирный	1700	1

розетка с заземляющим контактом; у знака — марка и ×N — число постов в рамке; группа щита, высота оси и назначение — в ведомости точек

знак разведён для читаемости: точка на стене — у выноски, привязка — до неё

граница зоны 2 ванной (600 мм от ванны/поддона)

мебель и сантехприборы — подложка

стояк: К1 — канализация, В1 — ХВС, Т3 — ГВС

1 — номер помещения, площадь м²

Итого розеток (механизмов) — 36 шт; рамок — 30 шт: на 1 пост — 24, на 2 поста — 6.


Примечания

1. За отметку 0,000 принят уровень чистого пола. Высоты Н — от чистого пола до оси изделия; привязки — от чистовой грани стены до оси механизма (у рамки на несколько постов — до оси рамки).
2. Высоты Н и группы щита — в ведомости электроточек: розетки — 300 мм от чистого пола до оси механизма, если в ведомости не указано иное; выводы кабеля — по паспорту прибора.
3. Розетки в санузле — только вне зон 0–2 (ПУЭ 7.1.48, ГОСТ Р 50571.7.701-2024), IP44, через УЗО 30 мА.
4. Розеточные и мокрые линии — через УЗО или дифавтомат с током утечки не более 30 мА (ПУЭ 7.1.79); в санузле выполнить ДСУП (ПУЭ 7.1.87–7.1.88).
5. Кабель — медный, исполнение нг(А)-LS (ГОСТ 31565-2012); скрытая прокладка только горизонтально и вертикально, фактические трассы зафиксировать исполнительной схемой до закрытия отделкой.
6. Расчёт нагрузок, токов КЗ, селективности и сечений — по проекту ЭОМ организации с допуском СРО; лист задаёт состав, расположение и группы.
7. Выводы кухонной техники — после утверждения проекта кухни (ориентировочно); привязки выводов даны от осей модулей гарнитура и пересматриваются вместе с проектом кухни.
8. Электрический тёплый пол проектом не предусмотрен; при решении заказчика устроить — отдельный лист «План тёплых полов»: контуры с отступом 100 мм от стен и мебели без ножек, датчик в гофре, терморегулятор, своя группа щита через УЗО 30 мА.

	Лист	№ док.	Подпись	Дата	Проект: Квартира 56 м²			М 1:40
Дизайнер	Кырлан А.С.			13.11.26	План розеток и электровыводов	Стадия	Лист	Листов
Проверил						П	43	92
Н. контр.								
Утв.								

выпуск 13.11.2026 № 568a382a0d · стр. 43 из 92

План слаботочных сетей (М 1:40)

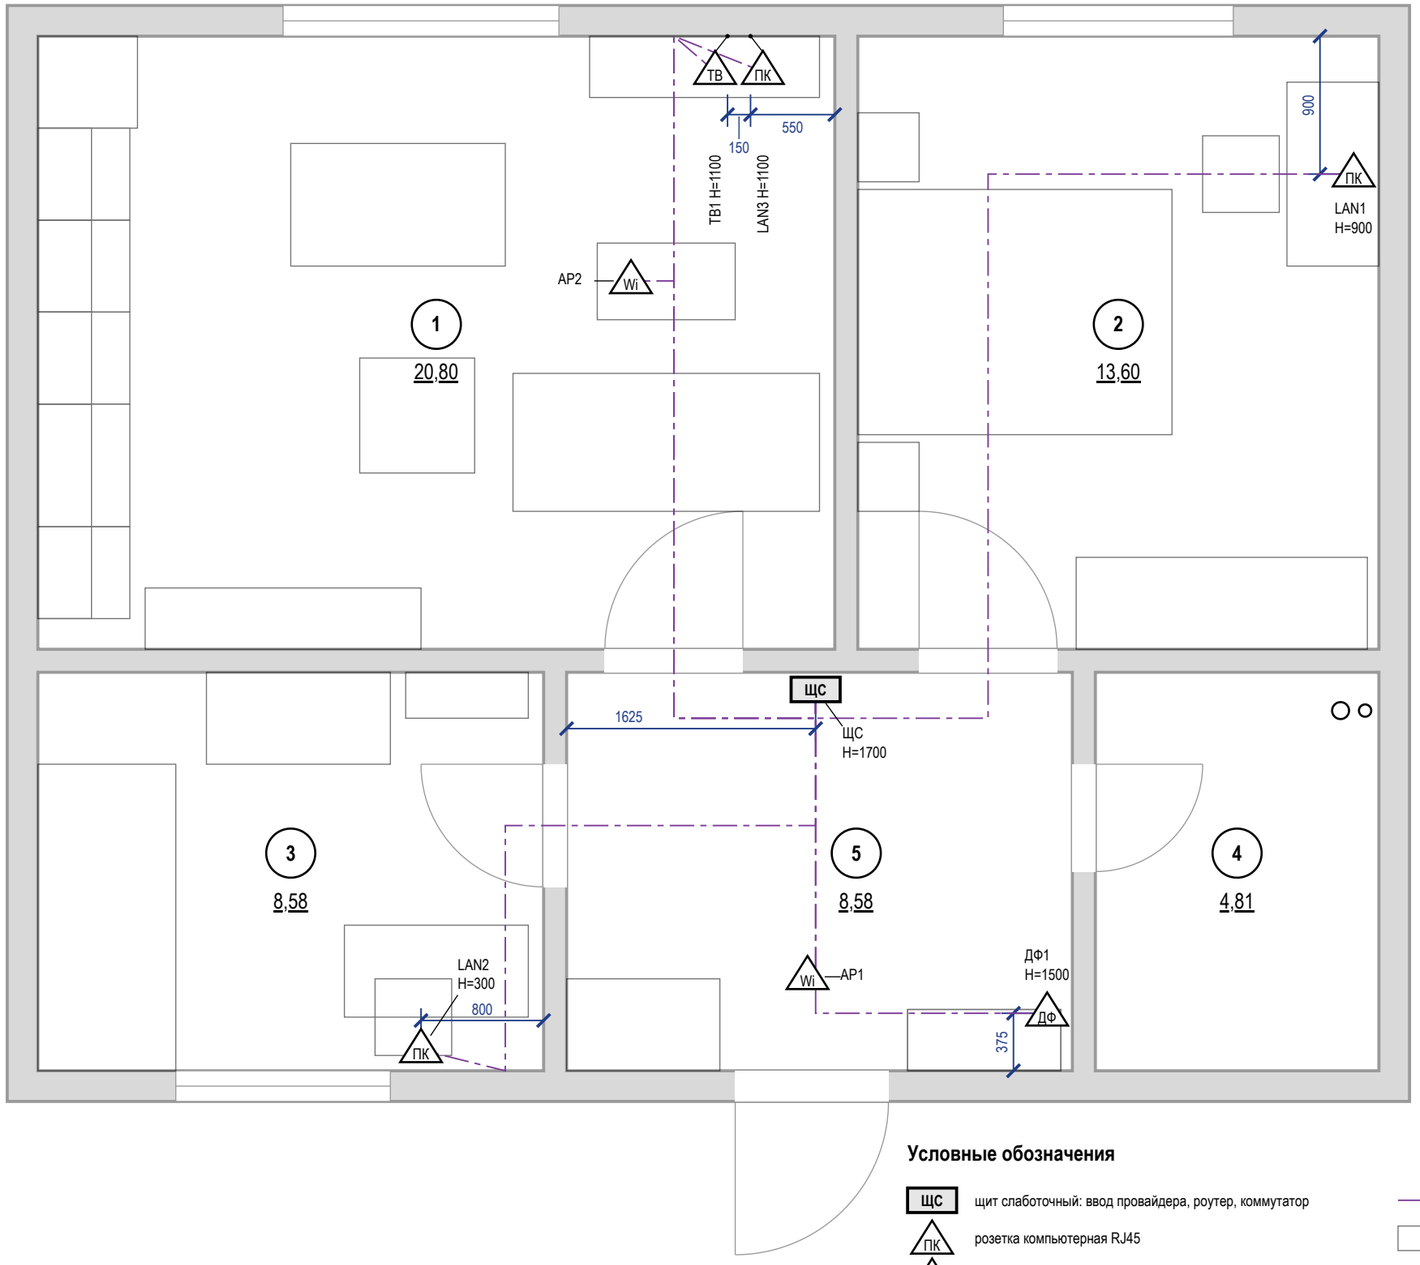

Условные обозначения

- ЩС — щит слаботочный: ввод провайдера, роутер, коммутатор
- ПК — розетка компьютерная RJ45
- ТВ — розетка телевизионная
- ДФ — трубка или монитор домофона
- Wi — точка доступа Wi-Fi (питание PoE)
- кабель от ЩС до точки, отдельным лучом
- мебель и сантехприборы — подложка
- стояк: К1 — канализация, В1 — ХВС, Т3 — ГВС
- 1 — номер помещения, площадь м²

Примечания

1. За отметку 0,000 принят уровень чистого пола. Высоты Н — от чистого пола до оси изделия; привязки — от чистовой грани стены до оси механизма (у рамки на несколько постов — до оси рамки).
2. Высота установки, не указанная на плане: розетки LAN и ТВ — 300 мм от чистого пола.
3. Слаботочные кабели — отдельно от силовых: в своей трубе или лотке, при параллельной прокладке не ближе 100 мм к силовым, пересечения под прямым углом; каждую точку — отдельным кабелем от ЩС без скруток.
4. Трассы на листе — принципиальные; фактические зафиксировать исполнительной схемой до закрытия отделкой. Силовые линии, УЗО 30 мА, ДСУП, кабель нг(А)-LS — по листам розеток и щита.
5. Проект силовой части и расчёт токов КЗ — по проекту ЭОМ; слаботочная часть согласуется с провайдером и управляющей компанией (домофон, коллективное ТВ).

	Лист	№ док.	Подпись	Дата
Дизайнер	Кырлан А.С.			13.11.26
Проверил				
Н. контр.				
Утв.				


Проект: Квартира 56 м² — М 1:40

План слаботочных сетей

Стадия	Лист	Листов
П	44	92

выпуск 13.11.2026 № 568a382a0d · стр. 44 из 92

План освещения (М 1:40)

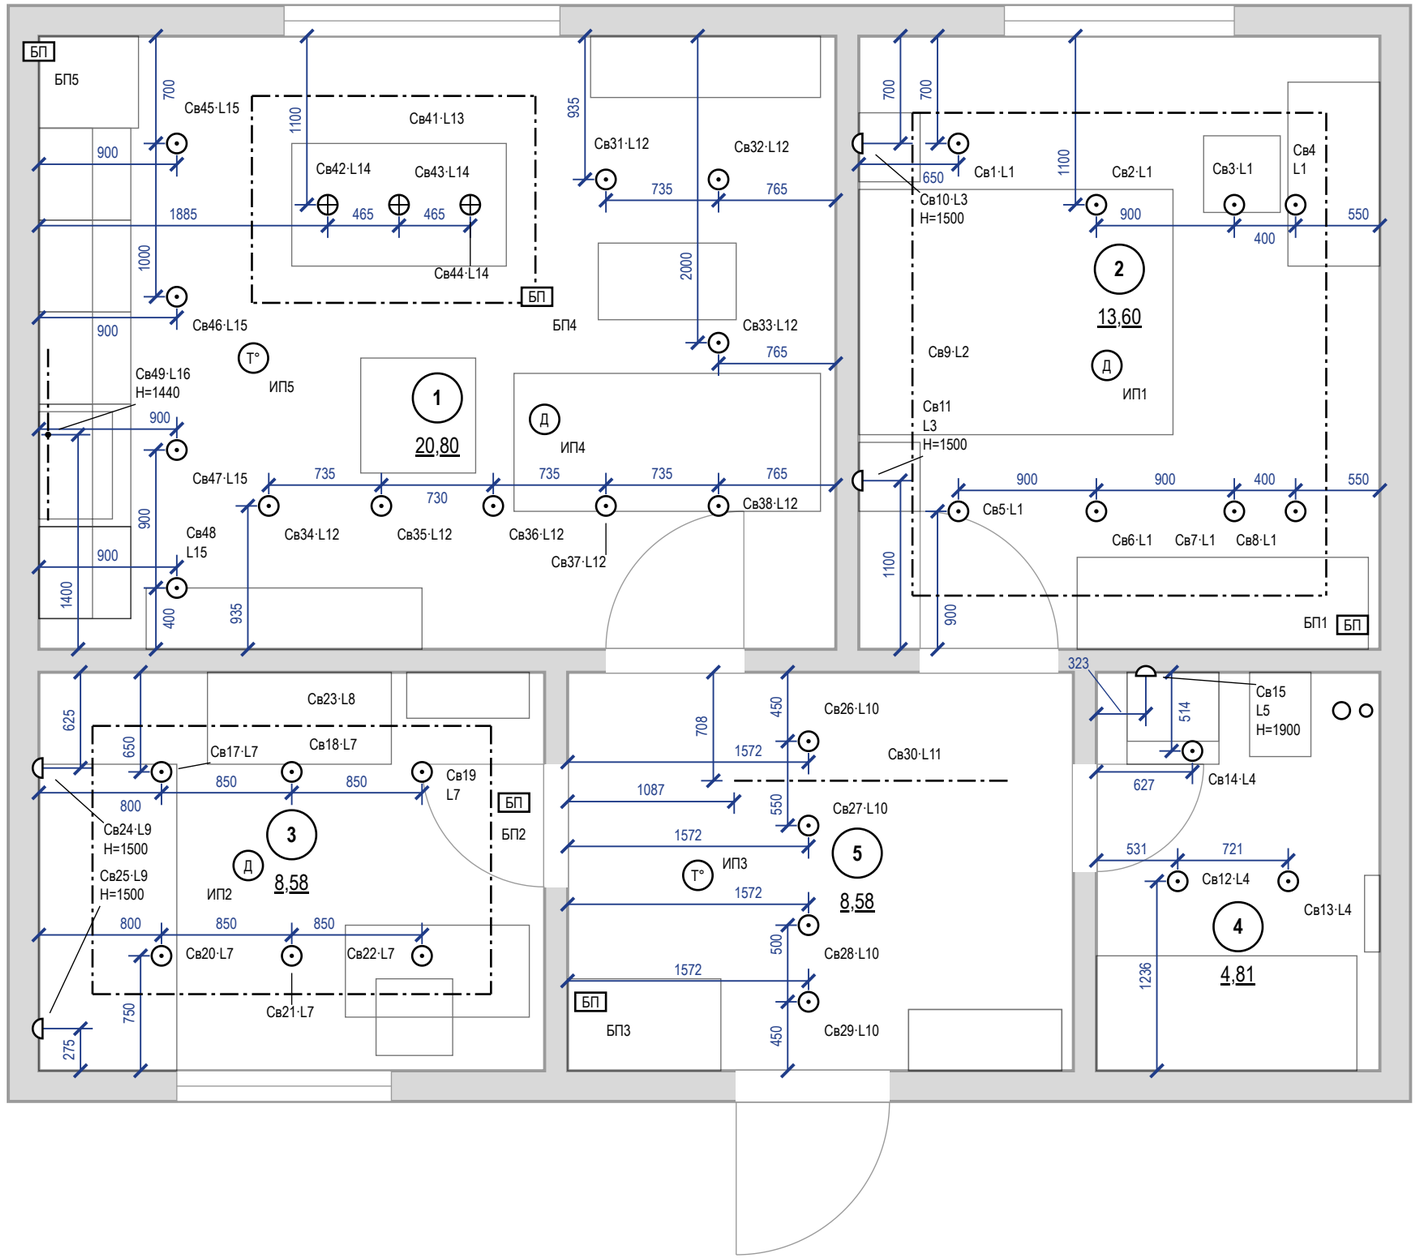

Условные обозначения

- светильник встраиваемый точечный
- светильник подвесной
- светильник настенный (бра), H — высота оси
- линейный светильник настенный (подсветка столешницы), точка — вывод питания
- светодиодная лента в профиле / в карнизе короба
- Св1·L1 — марка светильника (как в ведомости и на развёртках) · группа включения L (лист 47)
- Д — извещатель пожарный дымовой автономный
- Т° — извещатель пожарный тепловой
- БП — блок питания LED, с доступом (люк от 100×100 мм)
- мебель и сантехприборы — подложка
- стояк: К1 — канализация, В1 — ХВС, Т3 — ГВС
- 1 — номер помещения, площадь м²

Примечания

1. За отметку 0,000 принят уровень чистого пола. Высоты H — от чистого пола до оси изделия; привязки — от чистовой грани стены до оси механизма (у рамки на несколько постов — до оси рамки).
2. Высота установки, не указанная на плане: светильники — на потолке; настенные — по отметке H у знака. Привязки — до оси светильника от чистовой грани стены, по рядам.
3. Во влажных помещениях — светильники не ниже IP44; в зонах 0–2 ванной — по ГОСТ Р 50571.7.701-2024 (зона 1 — IPX5).
4. LED-лента в карнизе подсветки короба — по линии карниза с плана потолков; блок питания — в люке короба (БП на плане), питание ленты длиннее 5 м — с двух концов.
5. Розеточные и мокрые линии — через УЗО или дифавтомат с током утечки не более 30 мА (ПУЭ 7.1.79); в санузле выполнить ДСУП (ПУЭ 7.1.87–7.1.88).
6. Кабель — медный, исполнение нг(А)-LS (ГОСТ 31565-2012); скрытая прокладка только горизонтально и вертикально, фактические трассы зафиксировать исполнительной схемой до закрытия отделкой.
7. Расчёт нагрузок, токов КЗ, селективности и сечений — по проекту ЭОМ организации с допуском СРО; лист задаёт состав, расположение и группы.
8. Ведомость светильников (тип, количество, мощность, поток, Тц, Ra) — лист 46.

	Лист	№ док.	Подпись	Дата	Проект: Квартира 56 м²			М 1:40
Дизайнер	Кырлан А.С.			13.11.26	План освещения	Стадия	Лист	Листов
Проверил						П	45	92
Н. контр.								
Утв.								

выпуск 13.11.2026 № 568a382a0d · стр. 45 из 92

Параметры светильников для подбора

Поз.	Марки	Наименование	Установка	Кол.	P, Вт	Σ P, Вт	Ф, лм	Тц, К	Ra	Угол, °	IP	Дим.	Слой	Группа	Пом.
1	Св31, Св32, Св33, Св34, Св35, Св36, Св37, Св38	Встраиваемый точечный	в ГКЛ, корпус ≤ 70 мм	8	12	96	1000	3000	90	—	20	да	общий	L12	1
2	Св41	Лента светодиодная 24 В	в нише уровня, профиль с рассеивателем	6,4 м	9,6/м	61,4	900/м	2700	90	—	20	да	акцентный	L13	1
3	Св42, Св43, Св44	Подвесной	подвес, низ H=1450	3	9	27	800	3000	90	—	20	да	общий	L14	1
4	Св45–Св48	Встраиваемый точечный	в ГКЛ, корпус ≤ 70 мм	4	10	40	900	3000	90	—	20	—	общий	L15	1
5	Св49	Линейный настенный	под верхними шкафами, H=1440	1	18	18	1500	3000	90	—	20	да	рабочий	L16	1
6	Св1–Св8	Встраиваемый точечный	в ГКЛ, корпус ≤ 70 мм	8	12	96	1000	2700	90	—	20	—	общий	L1	2
7	Св9	Лента светодиодная 24 В	в карнизе короба, профиль с рассеивателем	11,7 м	9,6/м	112,3	900/м	2700	90	—	20	да	акцентный	L2	2
8	Св10, Св11, Св24, Св25	Настенный (бра)	на стене, H=1500	4	6	24	400	2700	90	60	20	—	рабочий	L3, L9	2, 3
9	Св17–Св22	Встраиваемый точечный	в ГКЛ, корпус ≤ 70 мм	6	12	72	1050	2700	90	—	20	—	общий	L7	3
10	Св23	Лента светодиодная 24 В	в карнизе короба, профиль с рассеивателем	8,7 м	9,6/м	83,5	900/м	2700	90	—	20	да	акцентный	L8	3
11	Св12–Св14	Встраиваемый точечный	в ГКЛ, корпус ≤ 70 мм	3	6	18	500	3000	90	—	44	—	общий	L4	4
12	Св15	Настенный светильник над зеркалом, драйвер встроен	над зеркалом, H=1900	1	8	8	600	3000	90	—	44	—	рабочий	L5	4
13	Св26–Св29	Встраиваемый точечный	в ГКЛ, корпус ≤ 70 мм	4	7	28	600	3000	90	—	20	—	общий	L10	5
14	Св30	Лента светодиодная 24 В	на поверхности, профиль с рассеивателем, датчик движения	1,8 м	4,8/м	8,6	150/м	2700	90	—	20	нет	ночной	L11	5
		Итого		**42 шт + 28,6 м**		**692,9**									

LED-ленты, линейные светильники и блоки питания

Марка	Пом.	L, м	U, В	Вт/м	Σ P, Вт	БП	P БП, Вт	Загр., %	Питание	Доступ к БП
Св41	1	6,4	24	9,6	61,4	БП4	300	20	с двух концов	люк 300×300 в нише фигуры потолка ПТ1
Св49	1	3	24	—	18	БП5	60	30	встроенный ввод	в колонне М-01 над нишей холодильника, верх, съёмная панель
Св9	2	11,7	24	9,6	112,3	БП1	200	56	с двух концов	люк 300×300 в коробе потолка ПТ1
Св23	3	8,7	24	9,6	83,5	БП2	200	42	с двух концов	люк 300×300 в коробе потолка ПТ1
Св30	5	1,8	24	4,8	8,6	БП3	20	43	с одного конца	в шкафу М-27, верхняя полка

Сценарии (помещения со светорегуляторами)


Помещение	Сценарий	Горят группы (уровень)	Управление
1. Гостиная-кухня	Вечер	L12 споты гостиной — 30 %; L13 подсветка короба — 100 %; L14 подвесы над столом — 50 %; остальные выкл.	светорегуляторы S7, S8, S12
	Ужин	L13 подсветка короба — 60 %; L14 подвесы над столом — 100 %; L16 подсветка столешницы — 30 %; остальные выкл.	светорегуляторы S8, S9, S12
	Кино	L13 подсветка короба — 20 %; остальные выкл.	светорегулятор S12
	Готовка	L12 споты гостиной — 50 %; L15 споты кухни — вкл.; L16 подсветка столешницы — 100 %; остальные выкл.	светорегуляторы S7, S9; выключатель S13

Примечания

1. Позиции и марки Св — те же, что на плане освещения (лист 45); группы L — по плану выключателей (лист 47).
2. Модели светильников не выбраны: лист — техническое задание на подбор. Модель по строке таблицы: поток, Тц, Ra, угол, IP и регулировка яркости не хуже указанных, мощность не больше; встраиваемые — под глубину короба (графа «Установка»). IP 20 — сухие помещения. После выбора моделей (артикул, производитель) лист выпускается как «Спецификация светильников».
3. Длина LED-ленты в карнизе и нише уровня — по линиям карниза и ниши плана потолков (лист 36); Σ P = Вт/м × длина. Блок питания загружен не больше чем на 80 %; лента 24 В длиннее 10 м питается с двух концов; доступ к блоку питания — люк ревизии 300×300 мм или место, указанное в таблице.
4. Сценарии: % — яркость группы на светорегуляторе; «вкл.» — группа на обычной клавише; группы, не названные в строке, выключены. Светильники и блоки питания групп на светорегуляторе — с регулировкой яркости. Клавиши и светорегуляторы — лист 47.
5. В пом. 2, 3 свет включается клавишами групп — лист 47.
6. Мощность и поток в таблице — требования к подбору (поток не меньше, мощность не больше указанных); после выбора модели — по её паспорту, Σ P — установленная мощность освещения. Оценка освещённости — на плане освещения; это не светотехнический расчёт.

	Лист	№ док.	Подпись	Дата	Проект: Квартира 56 м²			
Дизайнер	Кырлан А.С.			13.11.26				
Проверил					Техническое задание на подбор светильников	Стадия	Лист	Листов
Н. контр.								
Утв.						П	46	92

План выключателей (М 1:40)

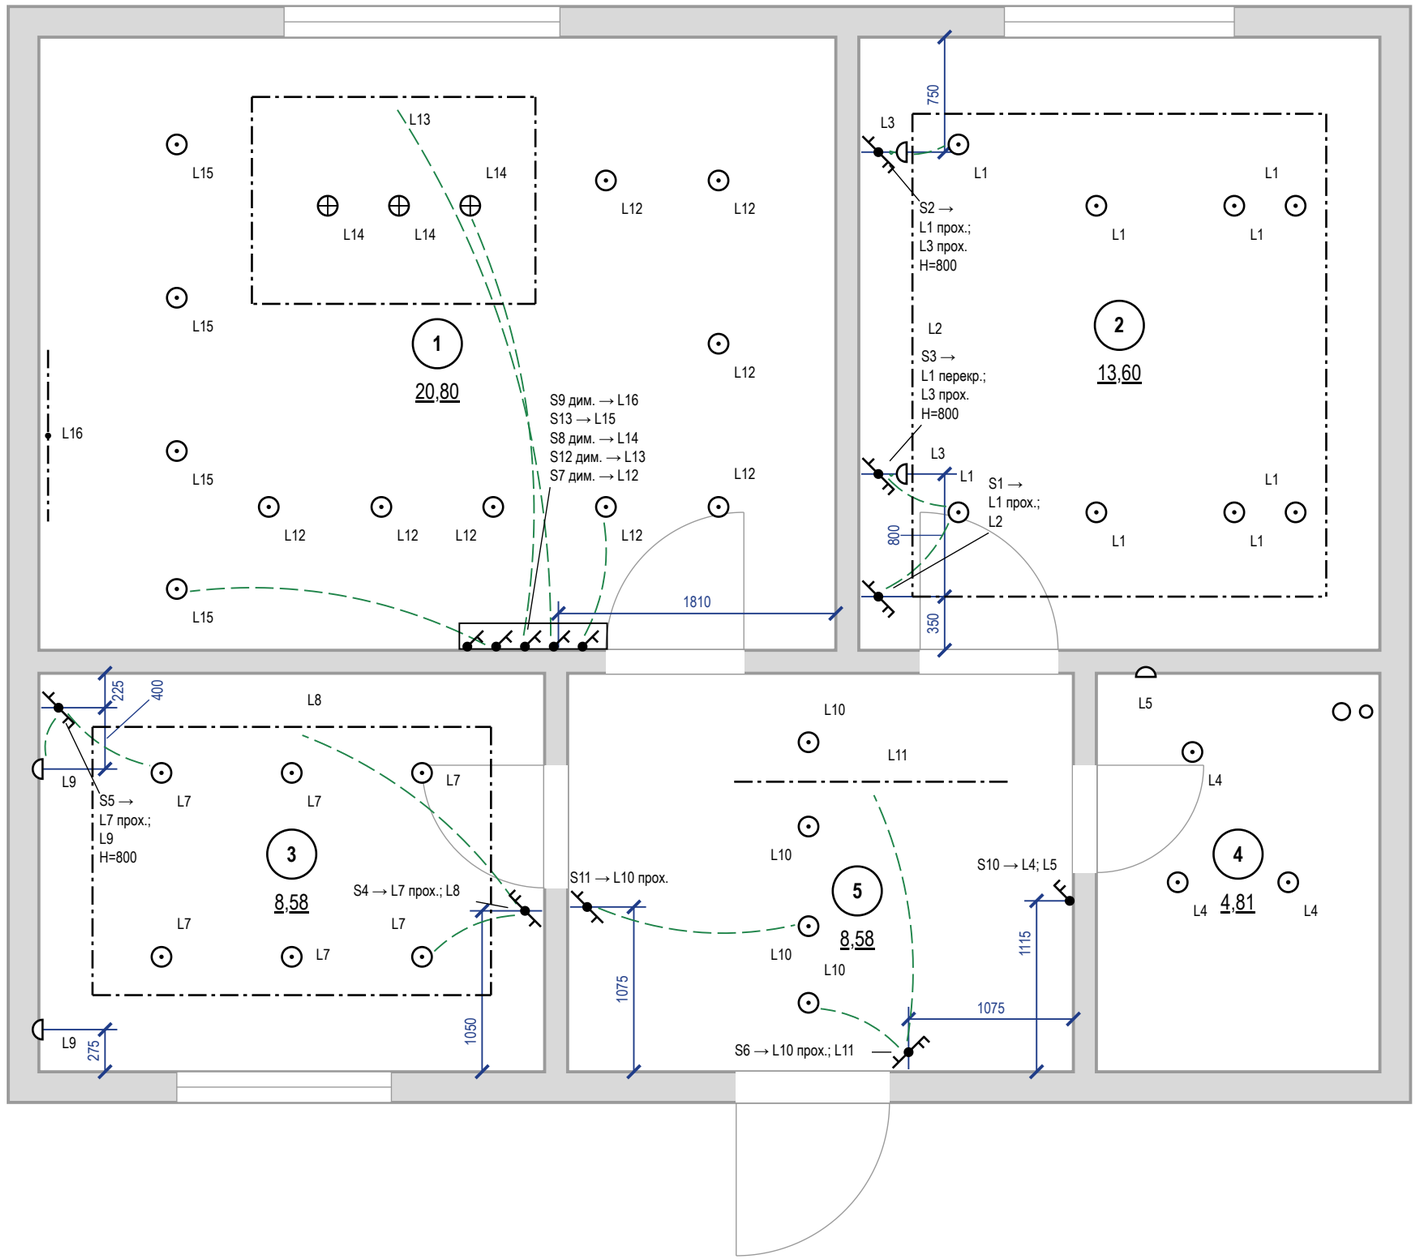

Условные обозначения


- выключатель одноклавишный
- выключатель двухклавишный (флажков — по числу клавиш)
- выключатель с проходной или перекрёстной клавишей (обратный флажок); тип клавиши — в подписи
- S1 → — марка → группы по клавишам (через «;»): прох. — проходной, перекр. — перекрёстный, дим. — светорегулятор; H — высота
- связь: выключатель → ближайший светильник группы в том же помещении (не трасса кабеля); полный состав группы — по номеру L
- светильник встраиваемый точечный
- светильник подвесной
- светильник настенный (бра), H — высота оси
- линейный светильник настенный (подсветка столешницы), точка — вывод питания
- светодиодная лента в профиле / в карнизе короба
- L1 — группа включения у светильника
- стояк: К1 — канализация, В1 — ХВС, Т3 — ГВС
- 1 — номер помещения, площадь м²

Примечания

1. За отметку 0,000 принят уровень чистого пола. Высоты H — от чистого пола до оси изделия; привязки — от чистовой грани стены до оси механизма (у рамки на несколько постов — до оси рамки).
2. Высота установки, не указанная на плане: выключатели — 900 мм от чистого пола (у кровати и другие — H у марки), со стороны дверной ручки (ПУЭ 7.1.51).
3. Какой выключатель какие светильники включает — по номеру группы L: у выключателя (S1 → L1; L2 — клавиши по порядку) и у каждого светильника. Пунктир — подсказка к ближайшему светильнику группы в том же помещении (не дальше 3 м), это не трасса кабеля; выключатель за стеной (у двери санузла) и далёкая группа только номер группы.
4. Группы из нескольких мест (L1 — S1, S2, S3; L3 — S2, S3; L7 S4, S5; L10 — S6, S11): на крайних местах — проходные клавиши, на промежуточных — перекрёстные; механизмы — в ведомости изделий.
5. Светорегулятор — по заднему фронту (для LED-драйверов), совместимость с драйверами проверить до закупки.
6. Розеточные и мокрые линии — через УЗО или дифавтомат с током утечки не более 30 мА (ПУЭ 7.1.79); в санузле выполнить ДСУП (ПУЭ 7.1.87–7.1.88).
7. Кабель — медный, исполнение нг(А)-LS (ГОСТ 31565-2012); скрытая прокладка только горизонтально и вертикально, фактические трассы зафиксировать исполнительной схемой до закрытия отделкой.
8. Расчёт нагрузок, токов КЗ, селективности и сечений — по проекту ЭОМ организации с допуском СРО; лист задаёт состав, расположение и группы.

	Лист	№ док.	Подпись	Дата	Проект: Квартира 56 м²		М 1:40	
Дизайнер	Кырлан А.С.			13.11.26				
Проверил					Управление светильниками	Стадия	Лист	Листов
Н. контр.						П	47	92
Утв.								

План вентиляции (М 1:40)

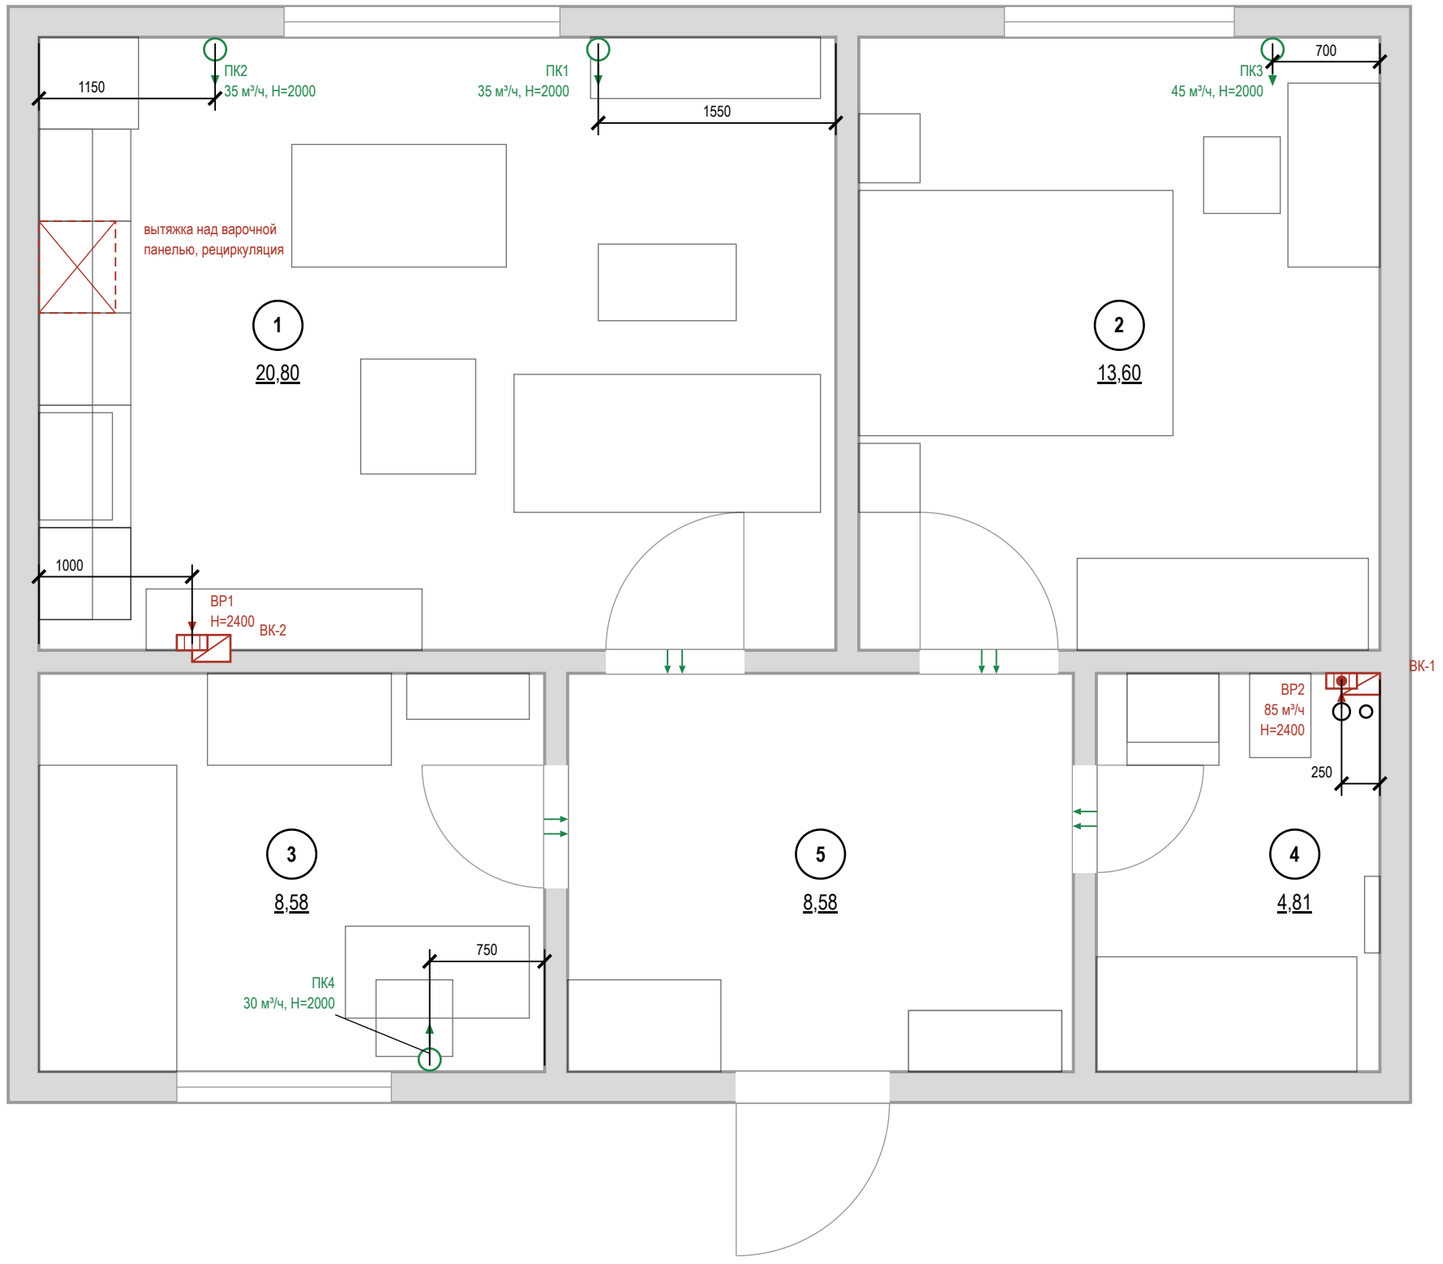

Условные обозначения

- стояк: К1 — канализация, В1 — ХВС, Т3 — ГВС
- номер помещения, площадь м²
- вытяжная решётка в вентканал: марка, расход м³/ч, H центра от чистого пола
- вытяжная решётка с бытовым вентилятором и обратным клапаном: марка, расход, H
- приточный клапан (КИВ) в наружной стене: марка, расход, H центра
- переток: зазор под полотном или переточная решётка
- кухонная вытяжка над варочной панелью
- Вентканал ВК-N.

Примечания

1. Воздухообмен по помещениям (норма / проект) и общие примечания к плану — лист 49.
2. Привязки — до обмера: вентканалы ВК-N приняты проектировщиком, решётки и воздуховоды — от них. До черновых работ — обмер каналов и тяги, лист перевыпустить по факту.

	Лист	№ док.	Подпись	Дата	Проект: Квартира 56 м²			М 1:40
Дизайнер	Кырлан А.С.			13.11.26	План вентиляции	Стадия	Лист	Листов
Проверил						П	48	92
Н. контр.								
Утв.								

выпуск 13.11.2026 № 568a382a0d · стр. 48 из 92

Воздухообмен, м³/ч

№	Помещение	Выт. норма	Выт. проект	Прит. норма	Прит. проект	Устрой-ства
1	Гостиная-кухня	60	60	63	70	ВР1, ПК1, ПК2
2	Спальня			41	45	ПК3
3	Детская			26	30	ПК4
4	Санузел	50	85			ВР2
	Итого	**110**	**145**	**130**	**145**	

Воздухообмен квартиры — по большей из сумм притока и вытяжки: норма 130 м³/ч, проект 145 м³/ч.
Вытяжка не меньше притока — баланс сведён.

Привязки — до обмера
Вентканалы ВК-N приняты проектировщиком, решётки и воздуховоды — от них. До черновых работ — обмер каналов и тяги, лист перевыпустить по факту.


Примечания

1. Марки устройств и кондиционеров — те же, что на плане вентиляции (лист 48); места, трассы и привязки — там же.
2. Расчёт систем ОВ и подбор оборудования — проектная организация с допуском СРО; лист даёт места, трассы и привязки.
3. Нормы вытяжки — СП 54.13330.2022 (Изм. 1, 2), табл. 7.1: кухня с электроплитой 60 м³/ч, с газовой 100; ванная и совмещённый санузел 50; уборная 25; гардеробная 0,2 ч⁻¹. Приток в жилые — 3 м³/ч на 1 м² (менее 20 м² общей площади на человека), иначе 30 м³/ч на человека.
4. Вентканалы и шахты не сужать, не переносить и не закрывать; вентилятор и кухонная вытяжка — через обратный клапан, без перекрытия естественной тяги.
5. Проектные расходы — не ниже нормы, вытяжка сведена с притоком вентиляторами мокрых помещений. Клапаны — в простенке у окна, центр 2000 мм, не над кроватью, не ближе 300 мм к стоякам отопления; типоразмер — на расход.
6. Гостиная-кухня (пом. 1): вытяжка над варочной панелью рециркуляционная — без воздуховода, короба и входа в канал, в воздухообмен не включена; естественная тяга через решётку канала сохраняется. Отвод в канал — только вариантом по реестру (после обмера канала).
7. Переток — зазор под полотнами межкомнатных дверей или переточная решётка.
8. Кондиционирование заданием не предусмотрено; при установке трассы фреона и дренажа (не менее 40 мм/м, в К1 через сифон) и питание заложить до черновых работ.
9. Привязки оборудования — по паспортам приобретённых моделей, до черновых работ.

	Лист	№ док.	Подпись	Дата	Проект: Квартира 56 м²			
Дизайнер	Кырлан А.С.			13.11.26				
Проверил					Ведомость воздухообмена	Стадия	Лист	Листов
Н. контр.								
Утв.						П	49	92

выпуск 13.11.2026 № 568a382a0d · стр. 49 из 92

План отопления (М 1:40)

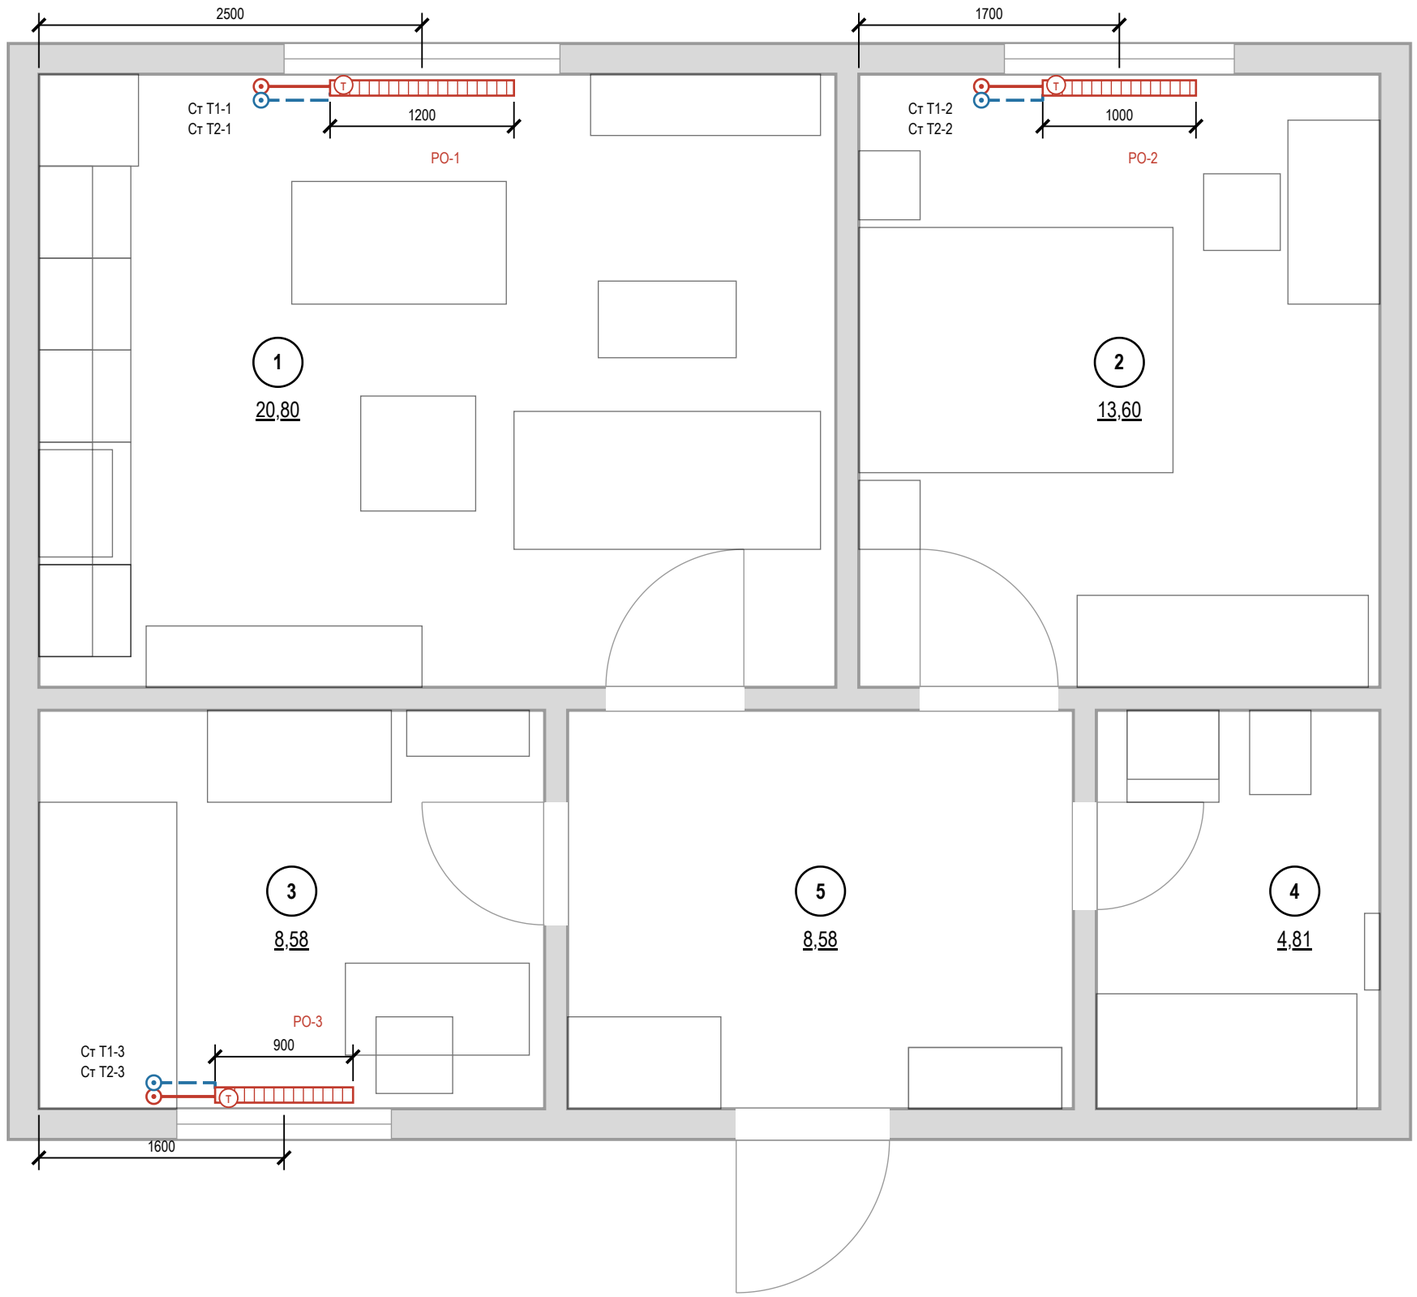

Условные обозначения

- 1 — номер помещения, площадь м²
- радиатор отопления (марка РО-N, длина по плану)
- Т — клапан с термоголовкой на подаче
- стояк отопления, подающий (Ст Т1-N)
- стояк отопления, обратный (Ст Т2-N)
- Т1 — отопление, подающий трубопровод
- Т2 — отопление, обратный трубопровод

Ведомость радиаторов

Марка	Помещение	Тип	Д×В×Г, мм	Низ / стена	Q, Вт
РО-1	1. Гостиная-кухня	панельный	1200×600×100	120 / 40	расч.
РО-2	2. Спальня	панельный	1000×600×100	120 / 40	расч.
РО-3	3. Детская	панельный	900×600×100	120 / 40	расч.


тип и мощность — по теплотехническому расчёту
Низ — от чистого пола, стена — зазор до задней панели, мм.

Привязки — до обмера
Стояки отопления в исходных данных не заданы: показаны у откосов окон, подводки — принципиально. До черновых работ — обмер стояков и паспорта приборов; лист перевыпустить по факту.




Примечания

1. Расчёт системы отопления, теплопотерь и подбор приборов — проектная организация с допуском СРО; лист даёт места и привязки.
2. Тип, длина и мощность радиаторов — по теплотехническому расчёту; лист задаёт места, зазоры и подключение.
3. Радиаторы — под каждым окном жилых комнат и кухни, центр по оси проёма, длина 0,7 ширины окна (кратно 100); окончательно — по расчёту.
4. Зазоры радиатора: низ не менее 100 мм от чистого пола, верх не менее 100 мм до подоконника, 30–50 мм от стены до задней панели; центр по оси окна с допуском ±20 мм. Верх до подоконника — 180 мм (РО-1 — 130).
5. Радиаторы не закрывать глухими коробами и мебелью; перенос и замена приборов в многоквартирном доме — переустройство, согласование с управляющей организацией (ЖК РФ ст. 25–26); вынос на лоджию запрещён.
6. Трубы отопления через межквартирные стены не прокладывать (СП 51.13330.2011, п. 9.19); через перекрытия и перегородки — в гильзах.
7. Привязки приборов и подводок — по паспортам приобретённых радиаторов и клапанов, до черновых работ.
8. До закрытия отделкой трубопроводы отопления испытать гидростатическим давлением с оформлением акта (СП 73.13330.2016, 7.2–7.3).

	Лист	№ док.	Подпись	Дата	Проект: Квартира 56 м²	М 1:40
Дизайнер	Кырлан А.С.			13.11.26	План отопления	Стадия: П; Лист: 50; Листов: 92
Проверил						
Н. контр.						
Утв.						

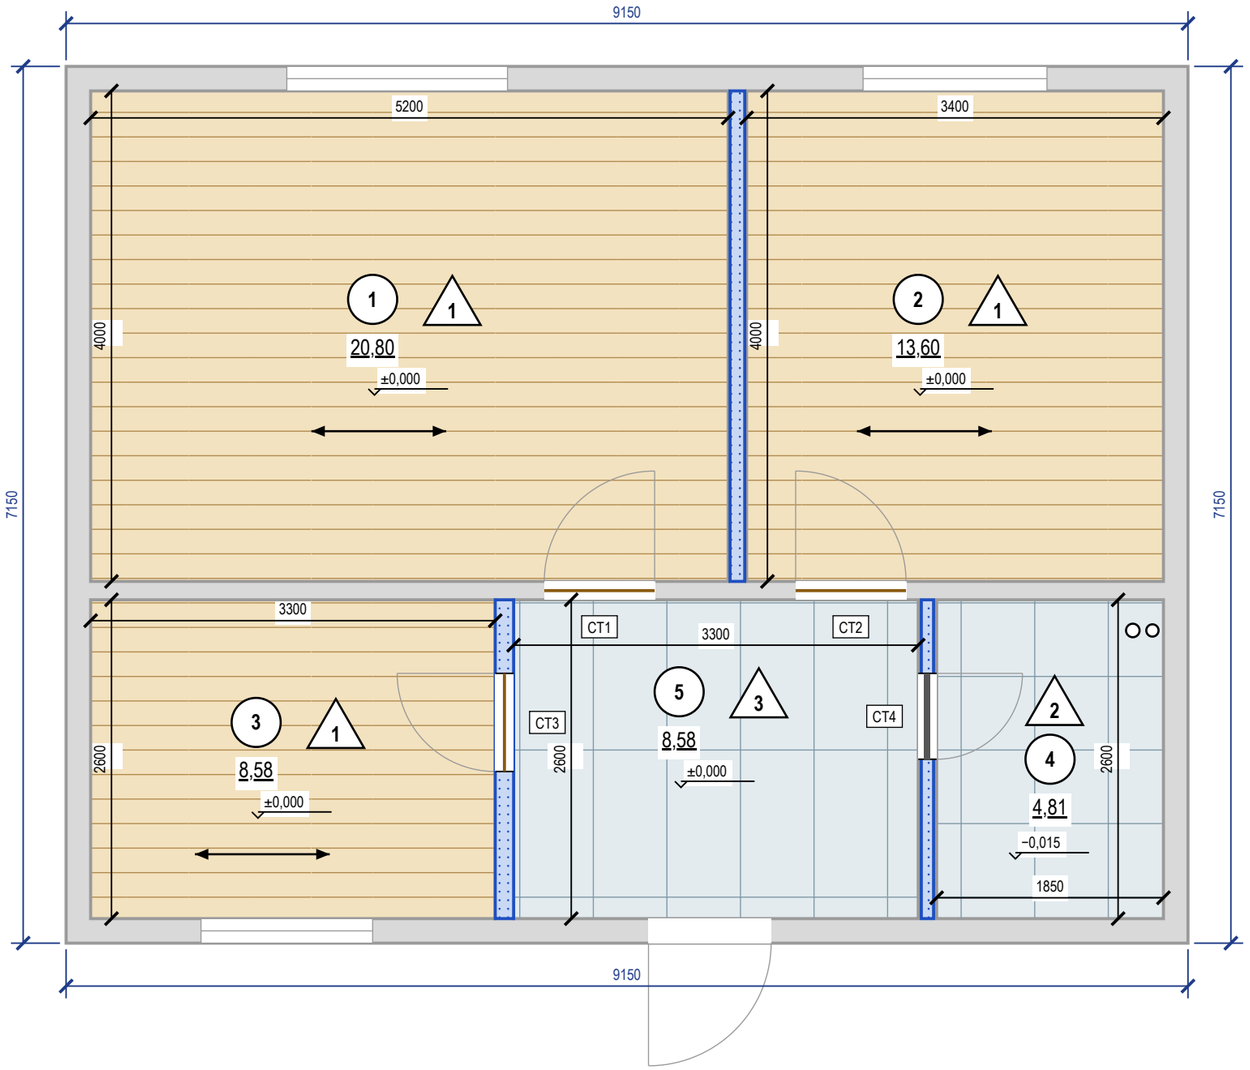

Экспликация полов

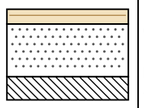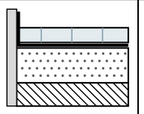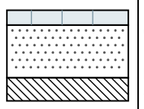Номер помещения	Тип пола	Схема пола	Данные элементов пола (наименование, толщина, основание), мм	Площадь, м²
1, 2, 3	1		Инженерная доска на клею — 14 Стяжка ЦПС М200 — 50 Плита перекрытия Всего 64 мм; ЧП ±0,000, верх плиты −0,064	42,98
4	2		Керамогранит на клею C2 TE S1 — 14 Гидроизоляция обмазочная, 2 слоя, с заведением на стены 200 мм — 2 Стяжка ЦПС М200 — 33 Плита перекрытия Всего 49 мм; ЧП −0,015, верх плиты −0,064	4,81
5	3		Керамогранит на клею C2 TE S1 — 14 Стяжка ЦПС М200 — 50 Плита перекрытия Всего 64 мм; ЧП ±0,000, верх плиты −0,064	8,58
			Итого	**56,37**

Раскладка покрытий

Пом.	Укладка	Старт (оси от чистовых стен), мм	Отступ 1-го ряда / крайние плитки, мм
1	вдоль стен A/B, прямая	от стены A, 1-й ряд вдоль неё	зазор от стены не задан
2	вдоль стен A/B, прямая	от стены A, 1-й ряд вдоль неё	зазор от стены не задан
3	вдоль стен A/B, прямая	от стены B, 1-й ряд вдоль неё	зазор от стены не задан
4	прямая, сетка 600×600, шов 2	ось X 901 от Г; ось Y 1276 от A	X 599 / 599; Y 372 / 372
5	плитка	раскладка плиточника не задана	

Спецификация плинтусов

Наименование	Помещения	Длина, м (с запасом)
Плинтус МДФ под покраску 80×16, крепление к стене, окраска в цвет NCS S 0804-Y30R	1, 2, 5	43
SX165, h = 69 мм, крепление к стене, окраска в цвет NCS S 0804-Y30R	3	13

Отметки по высоте


±0,000 чистый пол пом. 1–3, 5; отсчёт высот
−0,015 чистый пол пом. 4, ниже на 15 мм
−0,064 верх плиты — расчёт, не замер (задание на обмер)
сущ. пол снимается до плиты; не замерен (задание на обмер)

Примечания

1. За отметку ±0,000 принят чистый пол, не существующий (блок отметок). Площади — по чистым размерам помещений, м²; размеры — в мм.
2. Стык разнотипных покрытий — по оси дверного полотна (под полотном в закрытом положении); решение стыка — по ведомости стыков.
3. Пол санузлов ниже смежных помещений на 15 мм за счёт меньшей толщины стяжки (верх плиты общий — по экспликации полов); гидроизоляция по стяжке с заведением на стены не менее 200 мм (СП 29.13330.2011, п. 7.2), до облицовки — тест проливом и акт скрытых работ.
4. Трубопроводы в конструкции пола не прокладываются: пирог пола 49–64 мм не вмещает выпуски канализации с уклоном — выпуски К1 ведутся по стенам над чистым полом в коробах (лист 26).
5. Звукоизоляционный слой под стяжкой проектом не предусмотрен (стяжка по плите): приведённый уровень ударного шума перекрытия с полом Lnw не более 60 дБ (СП 51.13330.2011, табл. 2) подтвердить по данным дома; при превышении — плавающая стяжка по звукоизоляции с демпферной лентой по контуру и у стояков, пирог пересчитать.
6. Штучные покрытия (инженерная доска): направление — по стрелке; влажность основания по СМ не более 2,0 % (по ТУ изготовителя).
7. Ровность основания — просвет под 2-метровой рейкой не более 2 мм: пом. 1, 2, 3 (инженерная доска), пом. 4, 5 (керамогранит); проверить до укладки покрытия (СП 71.13330.2017, табл. 8.5).
8. Сетка на плитке — условная, в размер формата; точка старта и раскладка — по листу раскладки плитки.
9. Узор покрытия (заливка-код типа пола) прерывается под надписями — площадями помещений и отметками чистого пола.
10. Пироги полов — по экспликации полов: слои сверху вниз, толщины в мм; гидроизоляция мокрых зон — в пироге и в ведомости отделки; схема пола — без масштаба.

	Лист	№ док.	Подпись	Дата	Проект: Квартира 56 м²			М 1:50
Дизайнер	Кырлан А.С.			13.11.26	План покрытий пола	Стадия	Лист	Листов
Проверил						П	51	92
Н. контр.								
Утв.								

Фрагмент 1. Санузел (пом. 4). Пол 600×600, шов 2 мм (М 1:20)

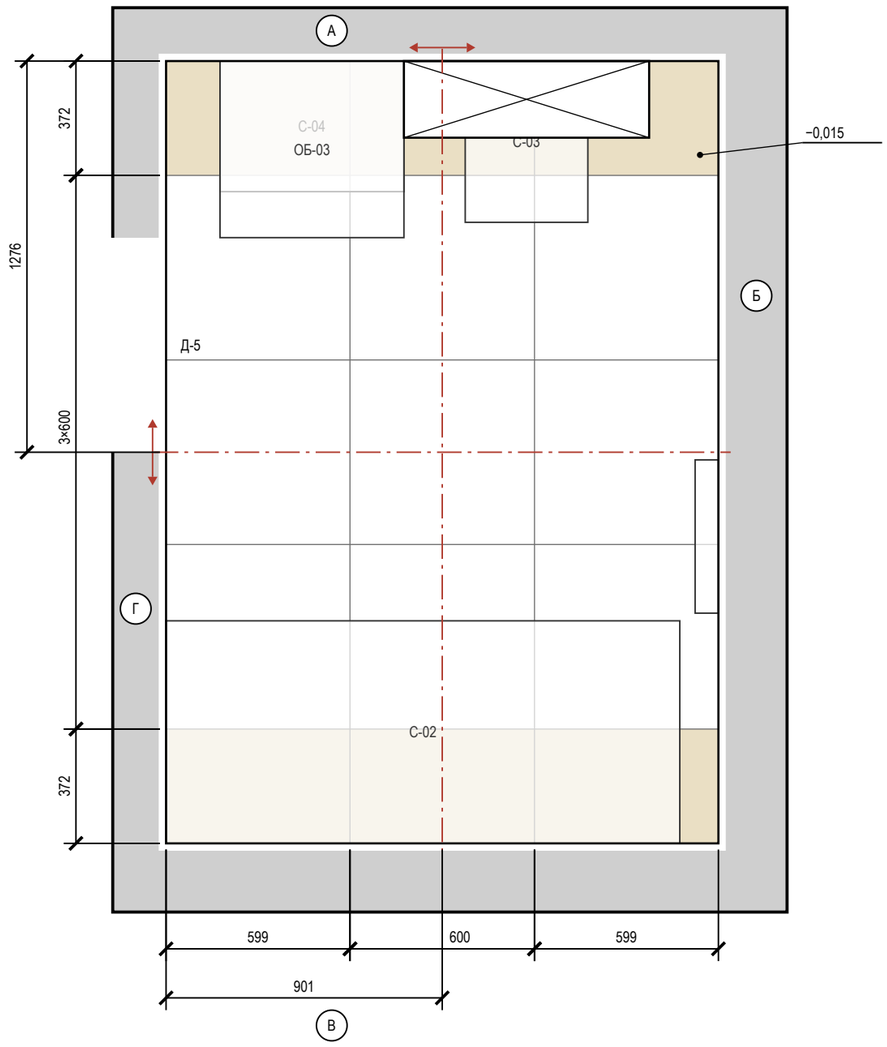

Ведомость плитки

Помещение, поверхность	Плитка, код	Формат	Шов	S, м²	Целых	Подр.	С запасом
Санузел, пол	аналог: керамогранит под травертин	600×600	2	4,81	9	6	17
Санузел, стены А–Г	A8UZ	600×1200	2	18,97	18	14	36
Санузел, короб инсталляции	A8UZ	600×1200	2	1,76	0	6	7
Прихожая, пол	A8UZ	600×1200	2	8,58	4	14	20
Гостиная-кухня, фартук (ст. Г)	аналог: керамогранит под травертин, матовый	1200×600	2	1,82	0	5	6
Итого 600×600				4,81	9	6	17
Итого 600×1200				**31,13**	**22**	**39**	**69**

Ведомость материалов

Материал	Класс, код	Норма расхода	Кол-во
Затирка	CG2WA Mapei Ultracolor Plus 132	(a+b)/ab·шов·t·1,6	2,1 кг
Затирка	CG2WA	(a+b)/ab·шов·t·1,6	0,8 кг
Клей	C2 TE S1 Ceresit CM 17	1,2 кг/м²·мм, слой 5	163 кг (7 меш.)
Клей	C2 TE S1	1,2 кг/м²·мм, слой 5	68 кг (3 меш.)
Гидроизоляция	обмазочная, 2 слоя: пол, стены по периметру и зоны замачивания	по ТУ	12,4 м²
Демпф. лента	по периметру пола из плитки		16,9 м

Условные обозначения

- плитка целая; тонкая линия — шов
- плитка с подрезкой (размер — на цепочке)
- ось старта; стрелки — направление укладки
- сантехприбор: габарит, высота по практике
- короб инсталляции: плитка пола — до короба
- отметка чистого пола на полке выноски, м
- А — обозначение стены А–Г (как на развёртках)


Примечания

1. Раскладка от чистовых размеров: стены санузлов теряют 10 + 5 + 9 = 24 мм на сторону (штукатурка, клей, плитка); подрезки — чистые, без шва.
2. Старт — от центра помещения (штрихпунктир, стрелки — направление укладки); размер старта — от чистовых стен Г и А.
3. Раскладка пола «Прихожая» и фартука «Гостиная-кухня» — на листе «Раскладка плитки. Прихожая. Фартук кухни».
4. Калибр партии не задан — до укладки замерить (рабочий размер W, ГОСТ 13996-2019) и пересчитать подрезки.
5. Количество: целые по раскладке + по одной на подрезку, запас 10 %; один артикул — одна партия и тон. Исключены поддон, короб, проёмы и места за коробом; S — по чистым граням: стены нетто = зона облицовки по ведомости отделки − место за коробом инсталляции 0,96 м² (плитку за коробом не кладут), короб — отдельной строкой.
6. Клей C2 TE S1 Ceresit CM 17; C2 TE S1 (ГОСТ Р 56387-2018), затирка CG2WA Mapei Ultracolor Plus 132; CG2WA; расход — по ТУ выбранной марки.
7. Гидроизоляция: пол и стены 200 мм от ЧП; над ванной — до 2000 и 300 мм за борт (см. развёртки); акт скрытых работ, пролив 24 ч.
8. Швы пола совмещены со швами стены А; по периметру — демпферная лента.
9. Отметка чистого пола −0,015, порог 15 мм; стык с соседним покрытием — по оси полотна двери.


	Лист	№ док.	Подпись	Дата	Проект: Квартира 56 м²			М 1:20
Дизайнер	Кырлан А.С.			13.11.26	Раскладка плитки. Планы полов	Стадия	Лист	Листов
Проверил						П	52	92
Н. контр.								
Утв.								

выпуск 13.11.2026 № 568a382a0d · стр. 52 из 92

Фрагмент 1. Прихожая (пом. 5). Пол 600×1200, шов 2 мм (М 1:25)

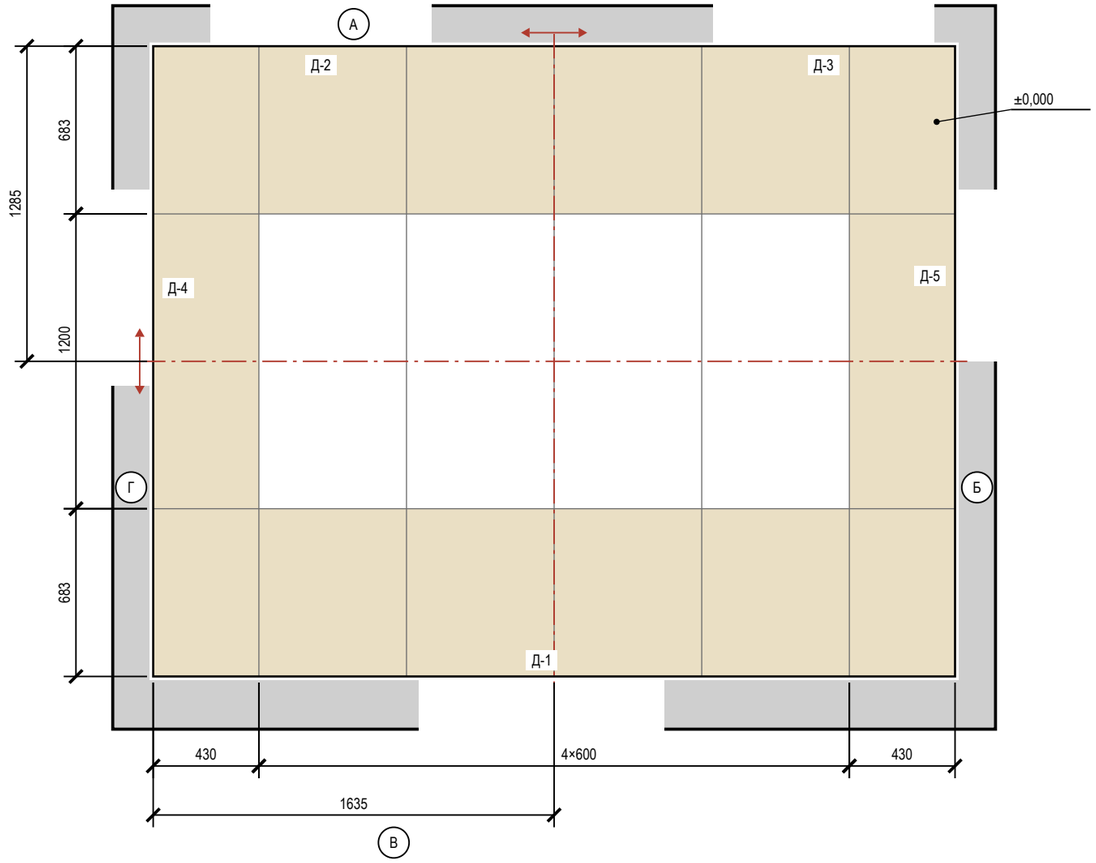

Фрагмент 2. Гостиная-кухня (пом. 1), фартук, стена Г. 1200×600, шов 2 мм (М 1:25)

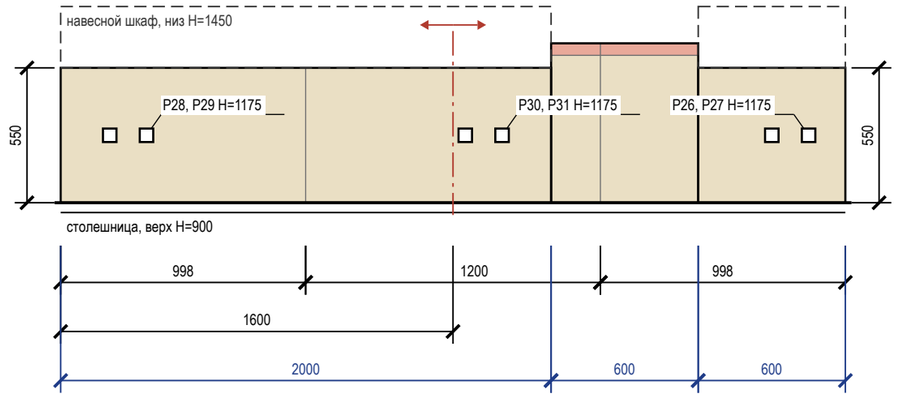

Условные обозначения

- плитка целая; тонкая линия — шов
- плитка с подрезкой (размер — на цепочке)
- ось старта; стрелки — направление укладки
- электроточка: марка и H — по листам ЭОМ
- столешница (верх)
- навесной шкаф над фартуком
- отметка чистого пола на полке выноски, м
- (А) обозначение стены А–Г (как на развёртках)

Подсчёт плитки

Поверхность	Формат	S, м²	Целых	Подр.	С запасом
Прихожая, пол	600×1200	8,58	4	14	20
Гостиная-кухня, фартук (ст. Г)	1200×600	1,82	0	5	6


Примечания

1. Прихожая: керамогранит 600×1200, длинная сторона — вдоль стен Б и Г, шов 2 мм, прямая раскладка от центра. Стены окрашены: раскладка от чистового контура минус штукатурка и шпаклёвка 15 мм на сторону (принято); подрезки 430 / 683 мм, срез — под плинтус.
2. Прихожая: деформационный зазор по периметру 8–10 мм под плинтусом; в проёмах — стык с соседним покрытием по оси полотна двери. Клей C2 TE S1, затирка CG2WA.
3. Фартук, Гостиная-кухня: 1200×600 горизонтально, шов 2 мм; зоны 600 мм — 900…1450, 600 мм — 900…1550, 2000 мм — 900…1450 (от столешницы до низа навесного шкафа, без шкафа — 650 мм). Старт от центра участка, подрезки 998 мм. Площадь 1,82 м² — как в ведомости отделки.
4. Фартук — после монтажа столешницы, низ на 2–3 мм выше неё, шов со столешницей — санитарный герметик; навесные шкафы — после фартука. Торцы у пенала и стены — профиль или запил 45°.
5. Фартук, Гостиная-кухня: в зоне до отм. 1550 верхний ряд подрезан 48 мм — меньше 1/3 плитки; полоса прикрыта корпусом навесного модуля и на виду не остаётся. Раскладкой не снимается: убрать подрезку можно, только выровняв низ этого модуля с соседними (1450 мм) — решение мебельщика.
6. Клей, затирка и итог по форматам — в ведомостях листа «Раскладка плитки. Планы полов».

	Лист	№ док.	Подпись	Дата	Проект: Квартира 56 м²			М 1:25
Дизайнер	Кырлан А.С.			13.11.26	Раскладка плитки. Прихожая. Фартук кухни	Стадия	Лист	Листов
Проверил						П	53	92
Н. контр.								
Утв.								

выпуск 13.11.2026 № 568a382a0d · стр. 53 из 92

Стена Г (М 1:20)

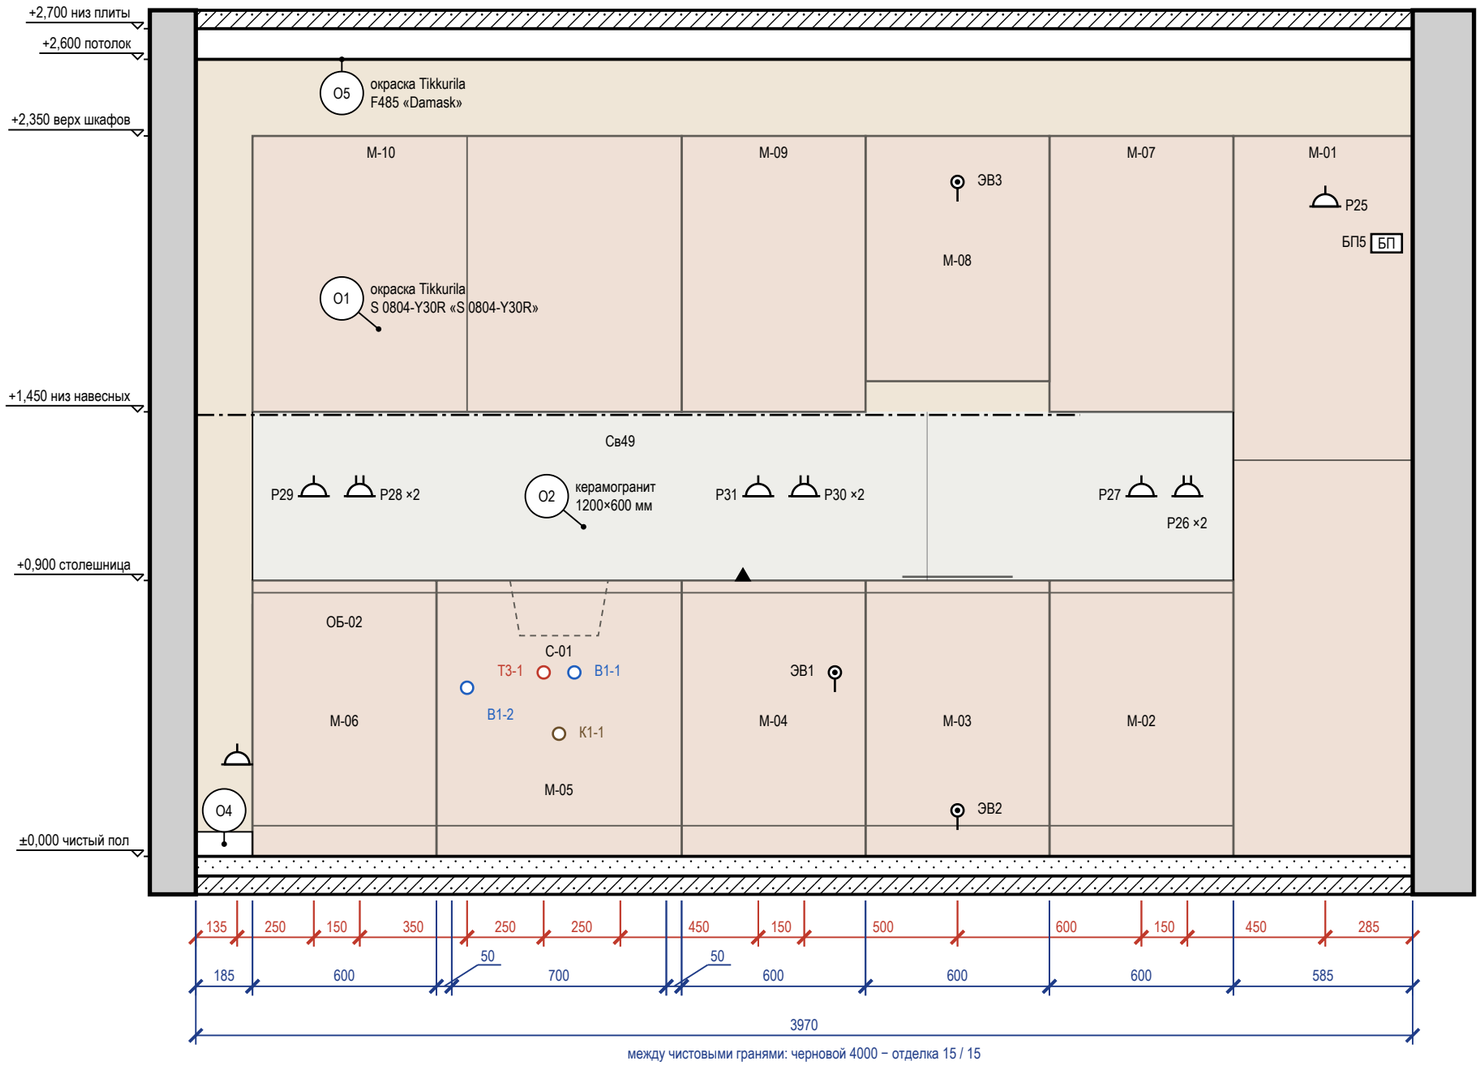


Ведомость точек и выводов

Марка	Что это	Гр.	Н, мм	От угла, мм	Примечание
Р32	розетка: посудомоечная машина (на стене за торцом гарнитура, доступ сбоку)	10	300	135	
Р29	розетка: фартук	7	1175	385	
Р28	розетка: фартук	7	1175	535	рамка 2 поста
В1-2	холодная вода — посудомоечная машина		550	885	кран ПММ в шкафу мойки
Т3-1	горячая вода — мойка кухонная		600	1135	межос. 100
К1-1	канализация — мойка кухонная		400	1185	Ø50
В1-1	холодная вода — мойка кухонная		600	1235	межос. 100
Св49	светильник настенный	2	1440	1385	лента -115–2885 от угла
Р31	розетка: фартук между мойкой и варочной	7	1175	1835	
Р30	розетка: фартук между мойкой и варочной	7	1175	1985	рамка 2 поста
ЭВ1	вывод кабеля: варочная панель — в соседнем модуле, за ящиком	8	600	2085	
ЭВ2	вывод кабеля: духовой шкаф	9	150	2485	
ЭВ3	вывод кабеля: вытяжка — над корпусом	11	2200	2485	
Р27	розетка: фартук	7	1175	3085	
Р26	розетка: фартук	7	1175	3235	рамка 2 поста
Р25	розетка: холодильник — над нишей, съёмная панель	11	2120	3685	
БП5	блок питания LED: в колонне М-01 над нишей холодильника, верх, съёмная панель	2	2000	3885	

Ведомость отделки (на листе)

Марка	Поверхность	Материал, изделие	Цвет, код	Кол.
О1	стены	окраска, Tikkurila Euro Power 7, колеровка по NCS, матовая, подготовка Q3	NCS S 0804-Y30R «S 0804-Y30R»	8,6 м²
О2	фартук	керамогранит, 1200×600×9 мм, аналог: керамогранит под травертин, матовый, затирка CG2WA		1,8 м²
О4	плинтус	плинтус МДФ, h 80 мм, аналог: плинтус МДФ под покраску 80×16	NCS S 0804-Y30R «S 0804-Y30R»	0,2 м
О5	потолок	окраска, Tikkurila Euro Power 7, глубокоматовая, подготовка Q3	Tikkurila F485 «Damask»	20,8 м²

Схема развёрток (М 1:200)

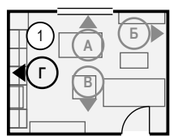

Примечания

1. Размеры — в мм от чистовых поверхностей стен; условные обозначения и общие указания — лист 10.
2. Схема мебели, приборов и декора не является технической документацией для производства мебели; габариты — по паспортам изделий.
3. Выводы ВК — коды и высоты по листу выводов сантехники.
4. Выводы кухонной техники — по утверждённому проекту кухни: привязки выводов даются от осей модулей гарнитура.
5. Потолок — у каждой стены свой, по плану потолков (ПТ2); ступени — зоной, кромка короба перед нишей — тонкой линией; в поле потолка: ПТ1 +2,500.
6. Часть марок не уместилась у знаков: коды, высоты и привязки этих позиций — в ведомости точек и выводов под видами.

	Лист	№ док.	Подпись	Дата	Проект: Квартира 56 м²	М 1:20		
Дизайнер	Кырлан А.С.			13.11.26	Развёртка стены Г. Гостиная-кухня (пом. 1), кухонный фронт	Стадия	Лист	Листов
Проверил						П	54	92
Н. контр.								
Утв.								

выпуск 13.11.2026 № 568a382a0d · стр. 54 из 92

Стена А (М 1:20)


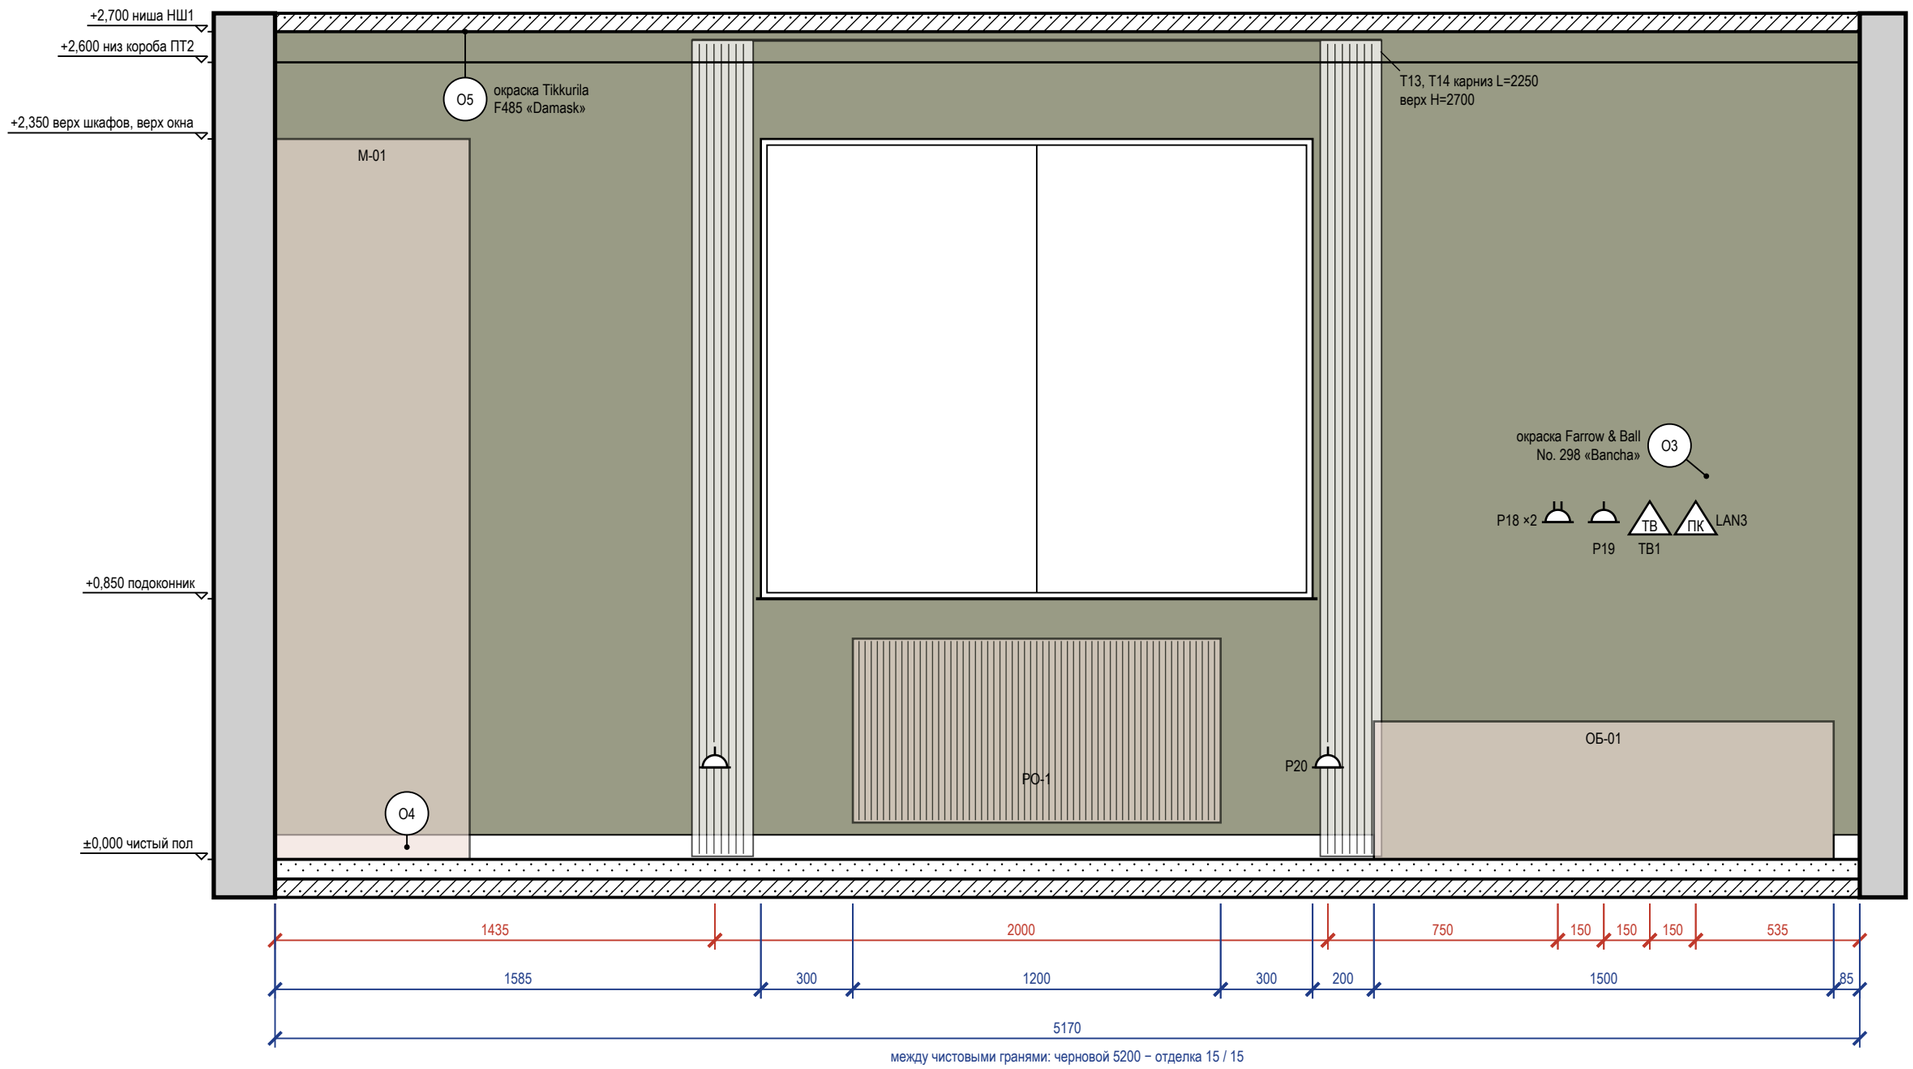


Схема развёрток (М 1:100)

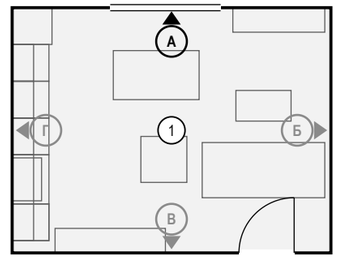

Ведомость точек и выводов

Марка	Что это	Гр.	H, мм	От угла, мм	Примечание
Р24	розетка: у обеденного стола	6	300	1435	
Р20	розетка: у ТВ-тумбы	6	300	3435	
Р18	розетка: ТВ (в одной зоне с ТВ1, LAN3)	6	1100	4185	рамка 2 поста
Р19	розетка: ТВ-приставка (в одной зоне с ТВ1, LAN3)	6	1100	4335	
ТВ1	розетка ТВ: ТВ-зона		1100	4485	
LAN3	розетка RJ45: Smart TV		1100	4635	

Ведомость отделки (на листе)

Марка	Поверхность	Материал, изделие	Цвет, код	Кол.
О3	акцентная стена	окраска, Farrow & Ball Modern Emulsion, матовая, подготовка Q3	Farrow & Ball No. 298 «Bancha»	11,3 м²
О4	плинтус	плинтус МДФ, h 80 мм, аналог: плинтус МДФ под покраску 80×16	NCS S 0804-Y30R «S 0804-Y30R»	3,7 м
О5	потолок	окраска, Tikkurila Euro Power 7, глубокоматовая, подготовка Q3	Tikkurila F485 «Damask»	20,8 м²

Примечания

1. Размеры — в мм от чистовых поверхностей стен; условные обозначения и общие указания — лист 10.
2. Карнизы (шины) — по ведомости текстиля декоратора: длина L и верх H на развёртке — те же числа, что в ведомости; крепление — до окраски потолка.
3. Потолок — у каждой стены свой, по плану потолков (НШ1, ПТ2); ступени — зоной, кромка короба перед нишей — тонкой линией; в поле потолка: ПТ1 +2,500.
4. Линии узора (швы плитки, складки штор, рёбра радиаторов) прерываются у знаков и выносок — просвет между линиями не менее 0,7 мм.
5. Часть марок не уместилась у знаков: коды, высоты и привязки этих позиций — в ведомости точек и выводов под видами.

	Лист	№ док.	Подпись	Дата	Проект: Квартира 56 м²			М 1:20
Дизайнер	Кырлан А.С.			13.11.26	Развёртка стены А. Гостиная-кухня (пом. 1)	Стадия	Лист	Листов
Проверил						П	55	92
Н. контр.								
Утв.								

выпуск 13.11.2026 № 568a382a0d · стр. 55 из 92

Стена Б (М 1:20)


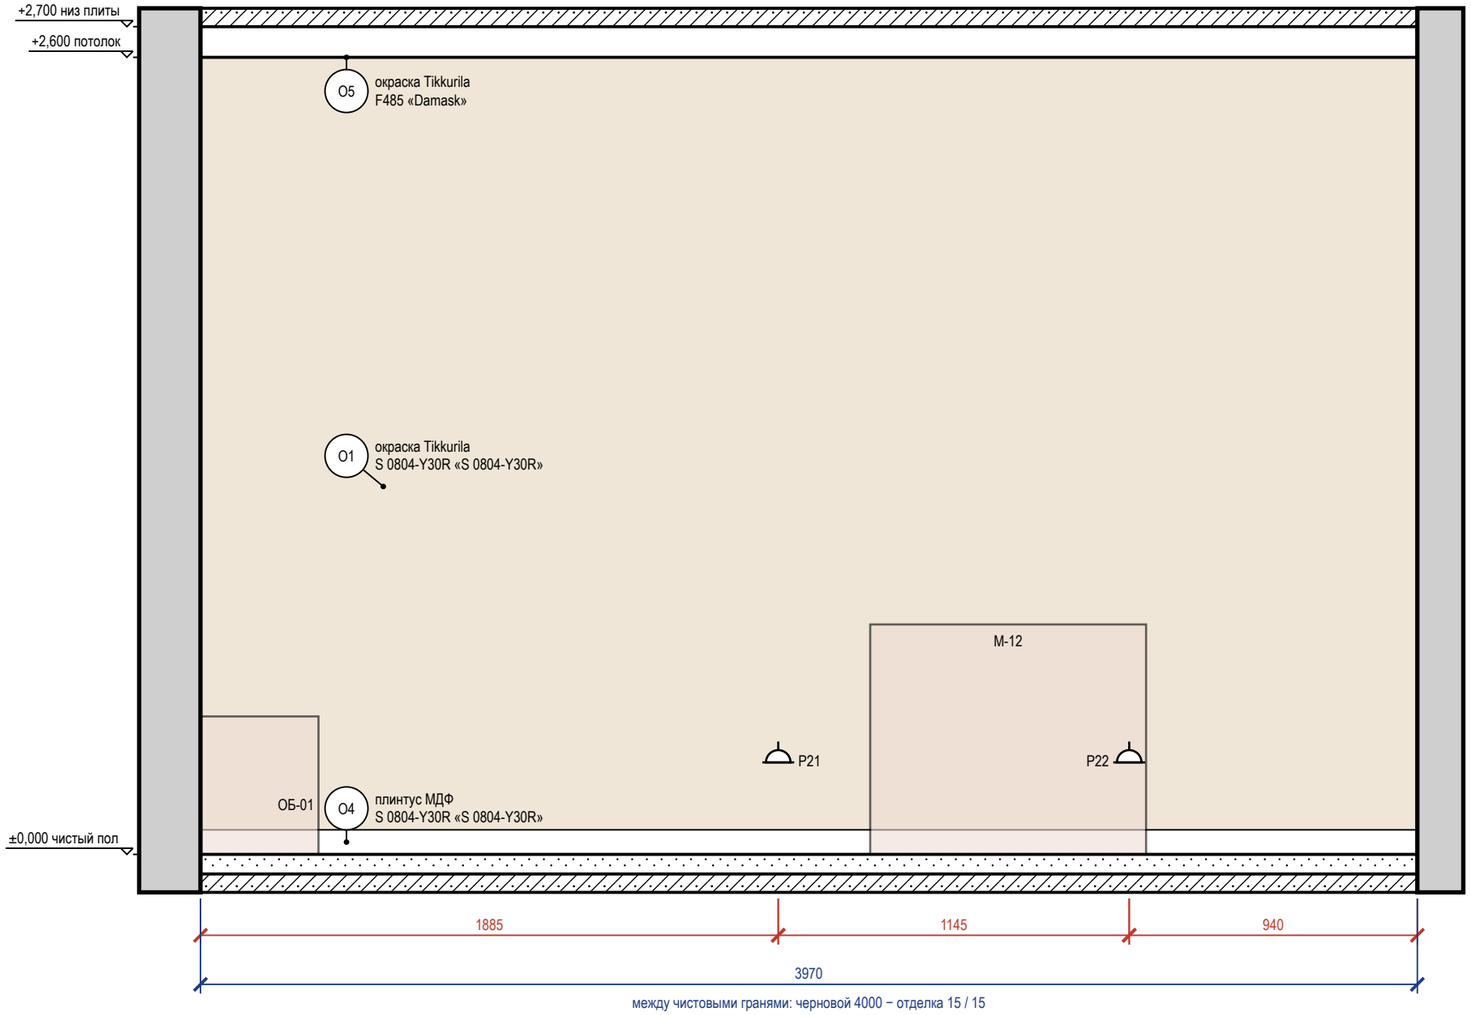


Схема развёрток (М 1:50)

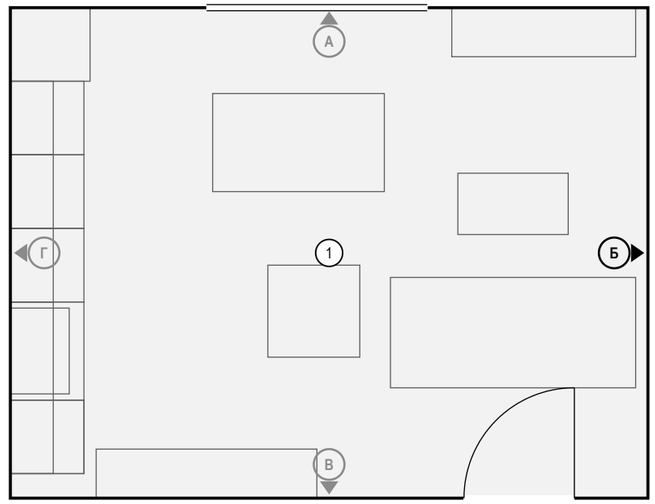

Ведомость точек и выводов

Марка	Что это	Гр.	Н, мм	От угла, мм	Примечание
Р21	розетка: торшер	6	300	1885	
Р22	розетка: у дивана	6	300	3030	

Ведомость отделки (на листе)

Марка	Поверхность	Материал, изделие	Цвет, код	Кол.
О1	стены	окраска, Tikkurila Euro Power 7, колеровка по NCS, матовая, подготовка Q3	NCS S 0804-Y30R «S 0804-Y30R»	10,3 м²
О4	плинтус	плинтус МДФ, h 80 мм, аналог: плинтус МДФ под покраску 80×16	NCS S 0804-Y30R «S 0804-Y30R»	4 м
О5	потолок	окраска, Tikkurila Euro Power 7, глубокоматовая, подготовка Q3	Tikkurila F485 «Damask»	20,8 м²

Ведомость изделий и проёмов (на листе)

Марка	Изделие, проём	На виде Ш×В, мм	Низ, мм
ОБ-01	тумба ТВ низкая, дуб, ТВ 55"	385×450	0
М-12	диван низкий 2000×900, лён, сиденье 400	900×750	0

Примечания

1. Размеры — в мм от чистовых поверхностей стен; условные обозначения и общие указания — лист 10.
2. Потолок — у каждой стены свой, по плану потолков (ПТ2); ступени — зоной, кромка короба перед нишей — тонкой линией; в поле потолка: ПТ1 +2,500.

	Лист	№ док.	Подпись	Дата
Дизайнер	Кырлан А.С.			13.11.26
Проверил				
Н. контр.				
Утв.				


Проект: Квартира 56 м² — **М 1:20**

Развёртка стены Б. Гостиная-кухня (пом. 1)

Стадия	Лист	Листов
П	56	92

выпуск 13.11.2026 № 568a382a0d · стр. 56 из 92


Стена В (М 1:25)

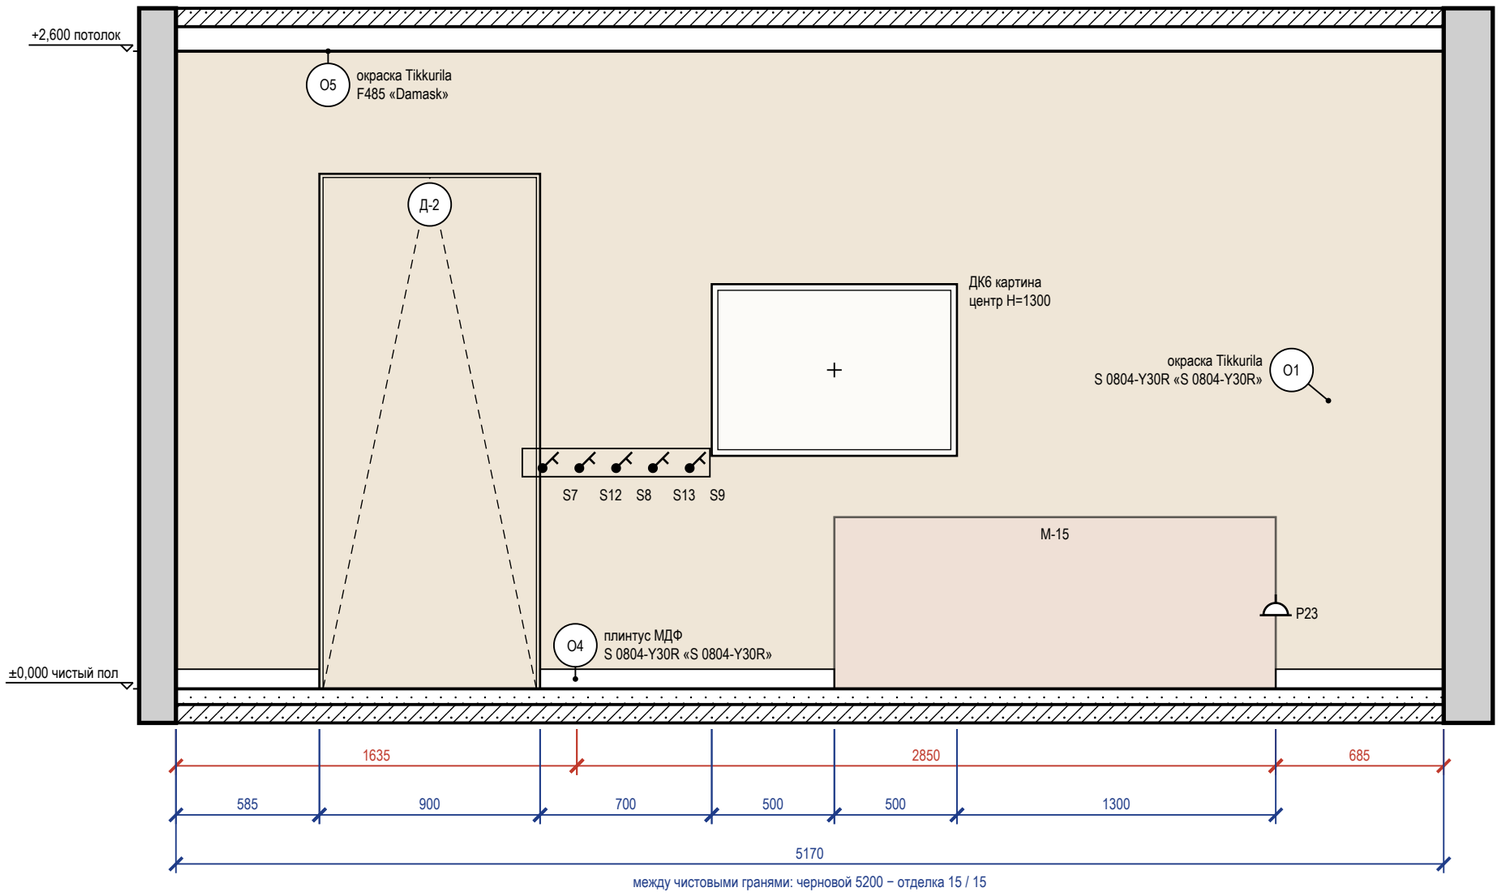

Стена В — визуализация, лист 4



Схема развёрток (М 1:50)

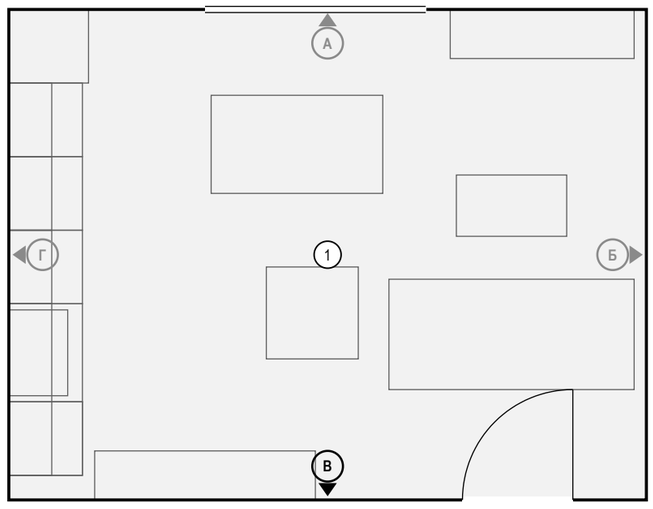

Ведомость точек и выводов

Марка	Что это	Гр.	H, мм	От угла, мм	Примечание
S7	выключатель	2	900	1635	
S12	выключатель	2	900	1715	
S8	выключатель	2	900	1795	
S13	выключатель	2	900	1875	
S9	выключатель	2	900	1955	
P23	розетка: уборка, пылесос	6	300	4485	

Ведомость отделки (на листе)

Марка	Поверхность	Материал, изделие	Цвет, код	Кол.
О1	стены	окраска, Tikkurila Euro Power 7, колеровка по NCS, матовая, подготовка Q3	NCS S 0804-Y30R «S 0804-Y30R»	11,6 м²
О4	плинтус	плинтус МДФ, h 80 мм, аналог: плинтус МДФ под покраску 80×16	NCS S 0804-Y30R «S 0804-Y30R»	2,5 м
О5	потолок	окраска, Tikkurila Euro Power 7, глубокоматовая, подготовка Q3	Tikkurila F485 «Damask»	20,8 м²

Ведомость изделий и проёмов (на листе)

Марка	Изделие, проём	На виде Ш×В, мм	Низ, мм
Д-2	дверь скрытого монтажа	900×2100	0
ДК6	картина	1000×700	950
М-15	консоль низкая 1800×400, тёмный ясень, фасады рифлёные	1800×700	0


Примечания

1. Размеры — в мм от чистовых поверхностей стен; условные обозначения и общие указания — лист 10.
2. Картины и зеркала крепить к основанию по паспорту изделия (закладные и анкеры — в перечне скрытых работ); крест — ось центра предмета.
3. Двери скрытого монтажа — полотно в плоскости стены, отделка стены по полотну, плинтус прерывается у короба (узел — на листе узлов).
4. Потолок — у каждой стены свой, по плану потолков (ПТ2); ступени — зоной, кромка короба перед нишей — тонкой линией; в поле потолка: ПТ1 +2,500.

	Лист	№ док.	Подпись	Дата	Проект: Квартира 56 м²	М 1:25		
Дизайнер	Кырлан А.С.			13.11.26				
Проверил					Развёртка стены В. Гостиная-кухня (пом. 1)	Стадия	Лист	Листов
Н. контр.						П	57	92
Утв.								

выпуск 13.11.2026 № 568a382a0d · стр. 57 из 92


Стена А (М 1:20)

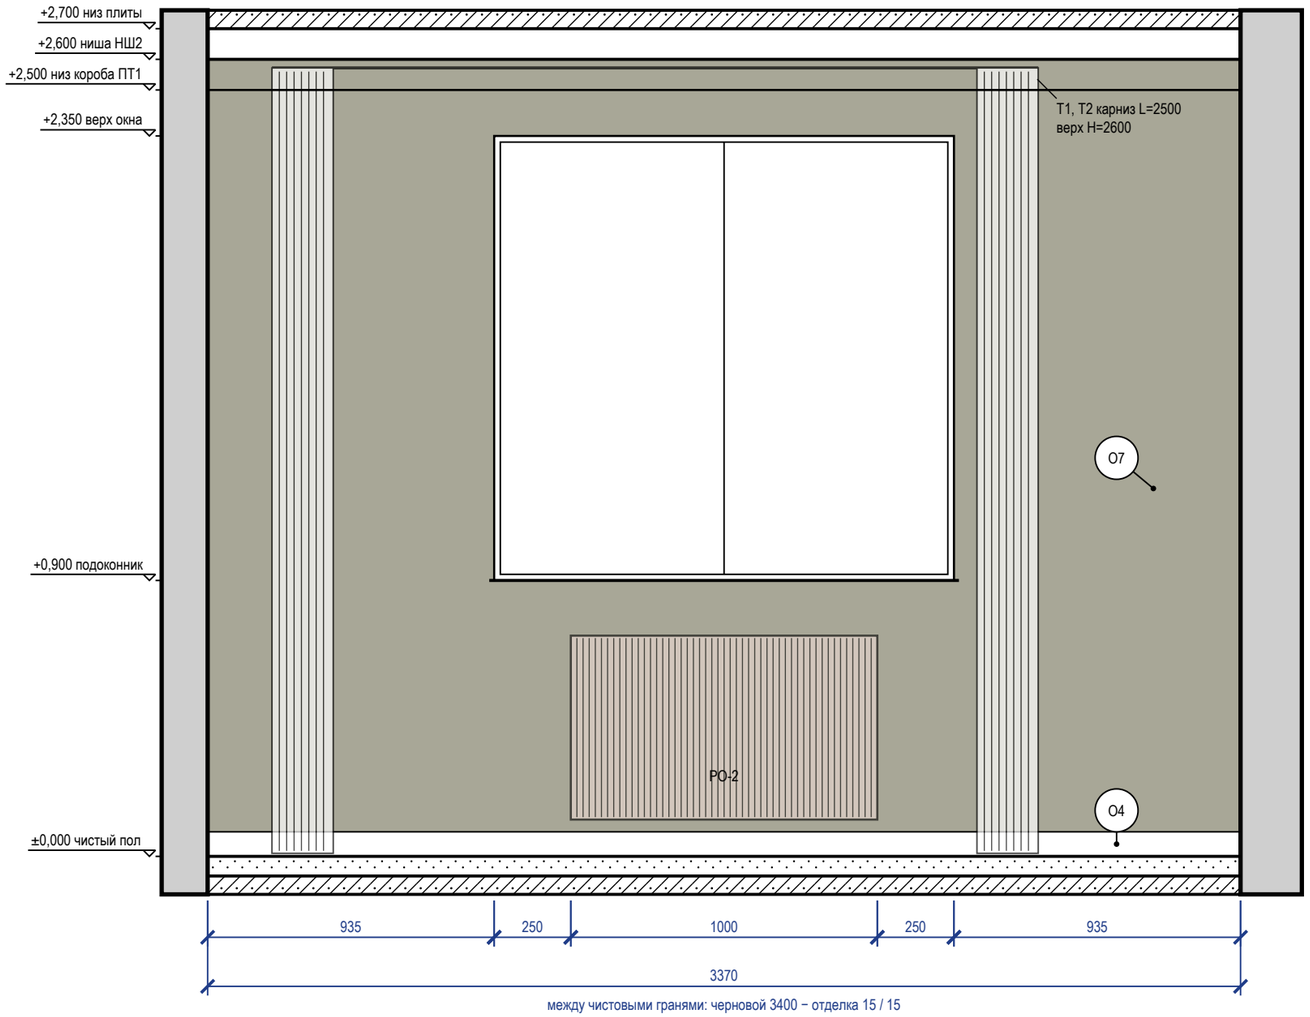

Стена А — визуализация, лист 5



Схема развёрток (М 1:50)

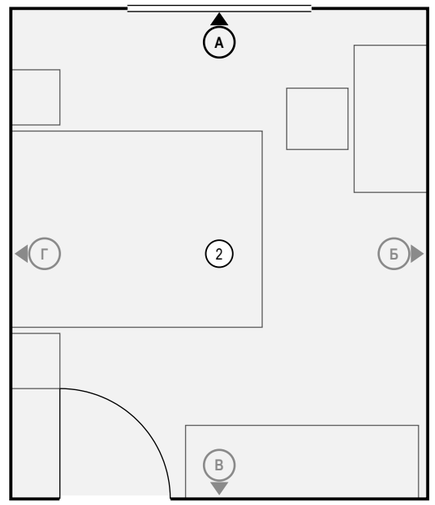

Ведомость отделки (на листе)

Марка	Поверхность	Материал, изделие	Цвет, код	Кол.
О4	плинтус	плинтус МДФ, h 80 мм, аналог: плинтус МДФ под покраску 80×16	NCS S 0804-Y30R «S 0804-Y30R»	3,4 м
О5	потолок	окраска, Tikkurila Euro Power 7, глубокоматовая, подготовка Q3	Tikkurila F485 «Damask»	13,6 м²
О7	акцентная стена	окраска, Tikkurila Euro Power 7, колеровка по NCS, матовая, подготовка Q3	NCS S 5010-G70Y «S 5010-G70Y»	6,6 м²

Ведомость изделий и проёмов (на листе)

Марка	Изделие, проём	На виде Ш×В, мм	Низ, мм
РО-2	радиатор отопления	1000×600	120

Примечания

1. Размеры — в мм от чистовых поверхностей стен; условные обозначения и общие указания — лист 10.
2. Карнизы (шины) — по ведомости текстиля декоратора: длина L и верх H на развёртке — те же числа, что в ведомости; крепление — до окраски потолка.
3. Потолок — у каждой стены свой, по плану потолков (НШ2, ПТ1); ступени — зоной, кромка короба перед нишей — тонкой линией; в поле потолка: ПТ2 +2,600.

	Лист	№ док.	Подпись	Дата
Дизайнер	Кырлан А.С.			13.11.26
Проверил				
Н. контр.				
Утв.				

Проект: Квартира 56 м² — **М 1:20**

Развёртка стены А. Спальня (пом. 2)

Стадия	Лист	Листов
П	58	92

выпуск 13.11.2026 № 568a382a0d · стр. 58 из 92

Стена Б (М 1:20)


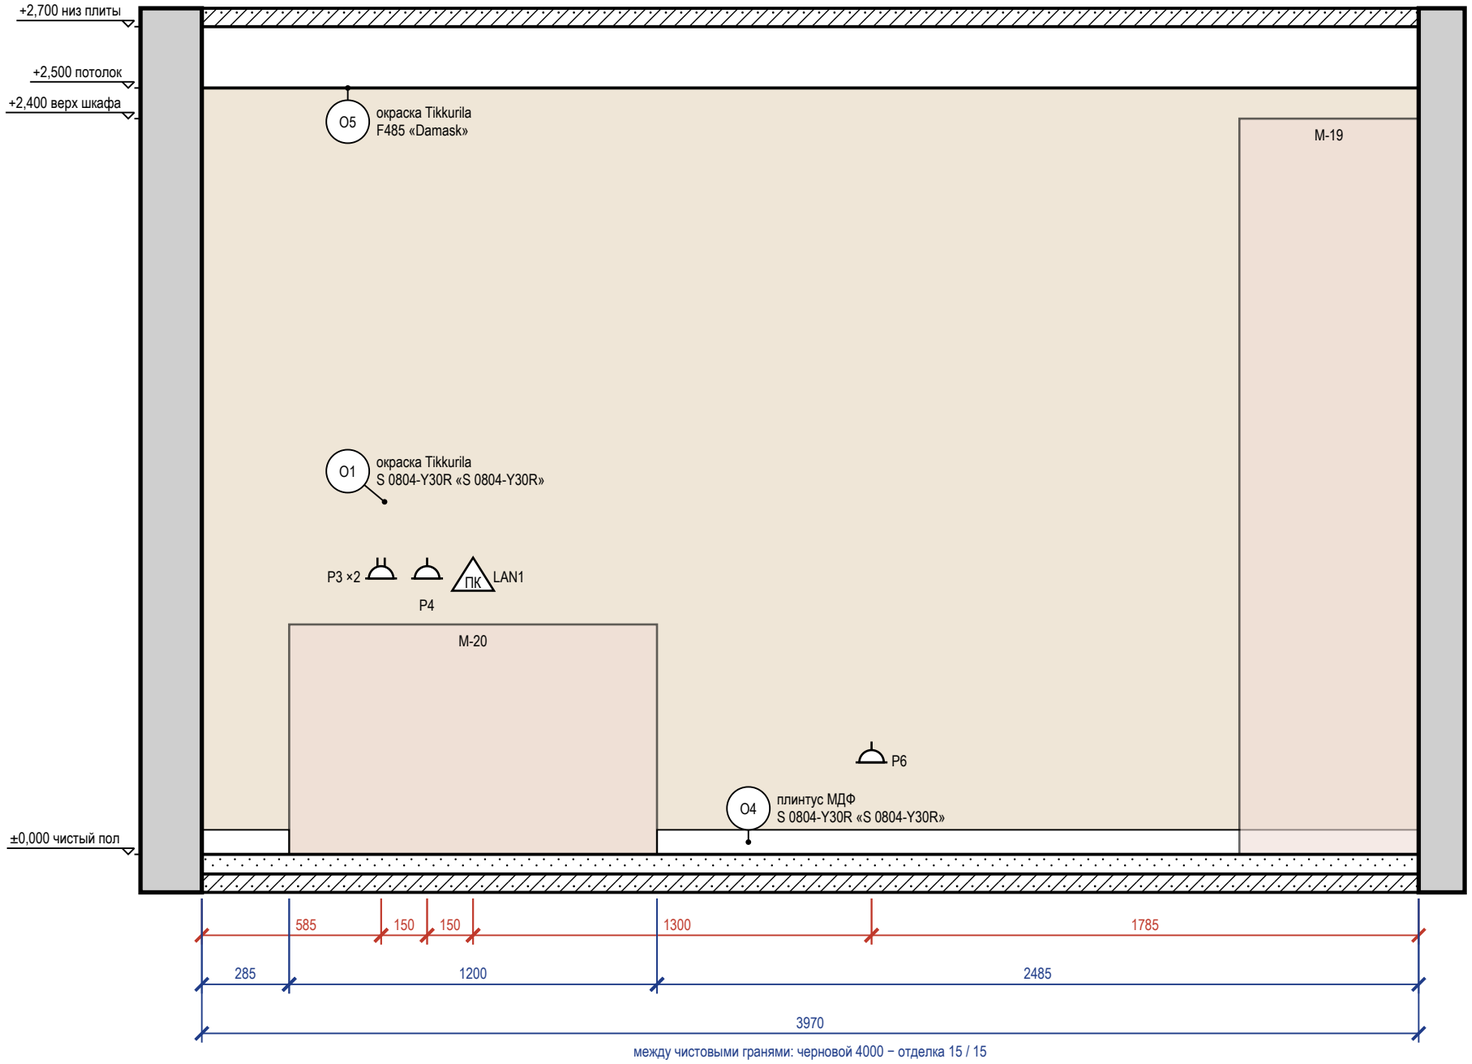


Схема развёрток (М 1:50)

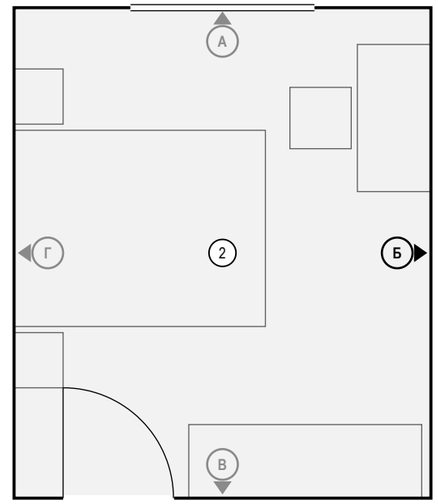

Ведомость точек и выводов

Марка	Что это	Гр.	Н, мм	От угла, мм	Примечание
Р3	розетка: рабочий стол	4	900	585	рамка 2 поста
Р4	розетка: рабочий стол	4	900	735	
LAN1	розетка RJ45: рабочий стол		900	885	
Р6	розетка: уборка	4	300	2185	

Ведомость отделки (на листе)

Марка	Поверхность	Материал, изделие	Цвет, код	Кол.
О1	стены	окраска, Tikkurila Euro Power 7, колеровка по NCS, матовая, подготовка Q3	NCS S 0804-Y30R «S 0804-Y30R»	9,9 м²
О4	плинтус	плинтус МДФ, h 80 мм, аналог: плинтус МДФ под покраску 80×16	NCS S 0804-Y30R «S 0804-Y30R»	2,8 м
О5	потолок	окраска, Tikkurila Euro Power 7, глубокоматовая, подготовка Q3	Tikkurila F485 «Damask»	13,6 м²

Ведомость изделий и проёмов (на листе)

Марка	Изделие, проём	На виде Ш×В, мм	Низ, мм
М-20	стол рабочий у окна 1200×600, дуб (работа из дома)	1200×750	0
М-19	шкаф распашной 1900×600 до 2400, фасады — дуб рифлёный	585×2400	0

Примечания

1. Размеры — в мм от чистовых поверхностей стен; условные обозначения и общие указания — лист 10.
2. Потолок — у каждой стены свой, по плану потолков (ПТ1); ступени — зоной, кромка короба перед нишей — тонкой линией; в поле потолка: ПТ2 +2,600.

	Лист	№ док.	Подпись	Дата
Дизайнер	Кырлан А.С.			13.11.26
Проверил				
Н. контр.				
Утв.				

Проект: Квартира 56 м² — **М 1:20**

Развёртка стены Б. Спальня (пом. 2)

Стадия	Лист	Листов
П	59	92

Стена В (М 1:20)


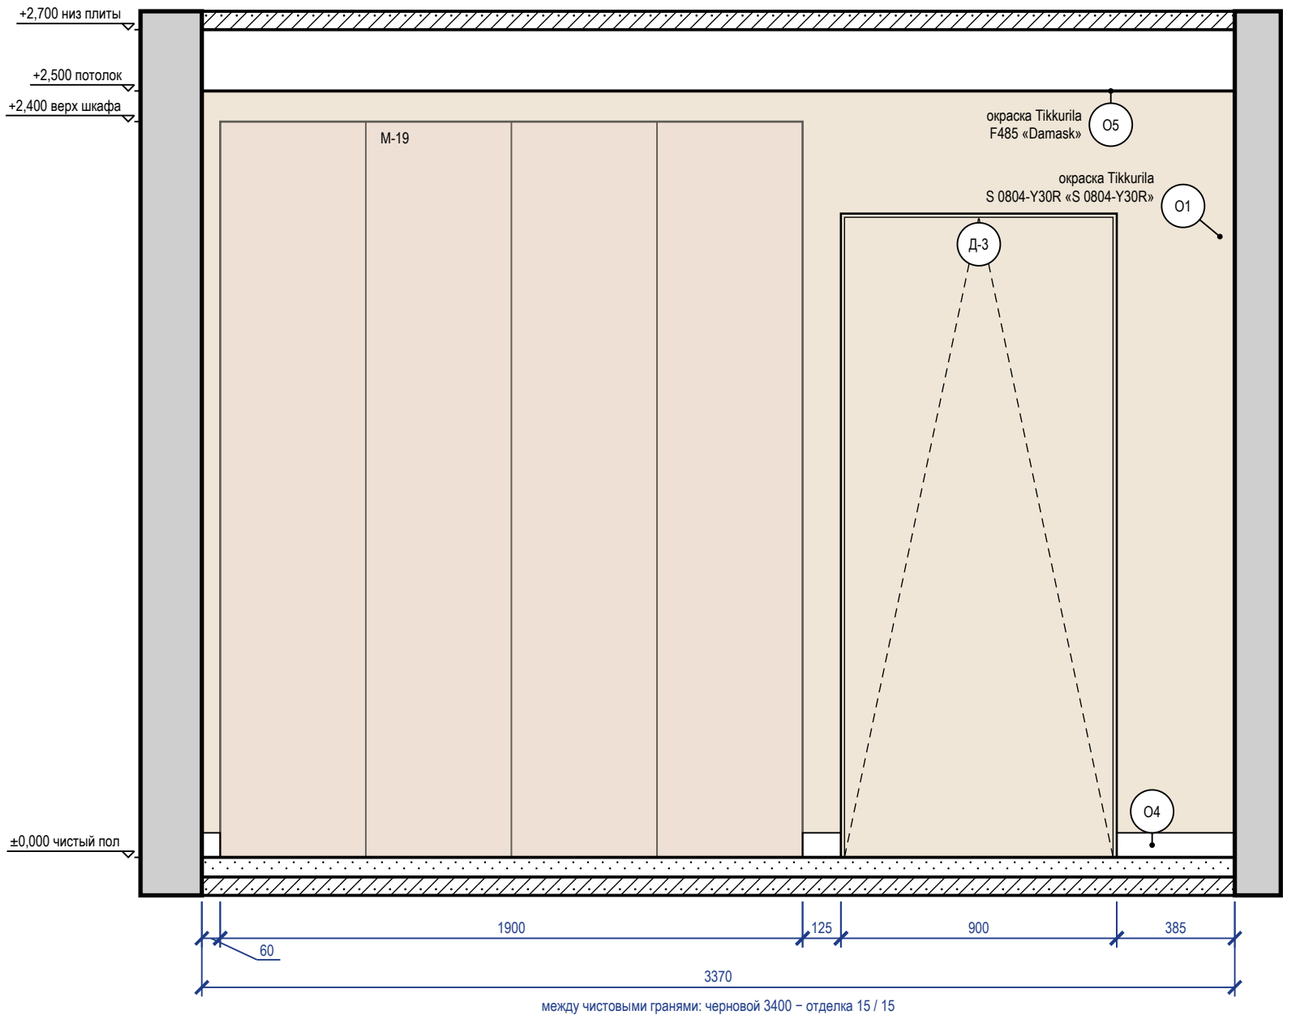


Схема развёрток (М 1:50)

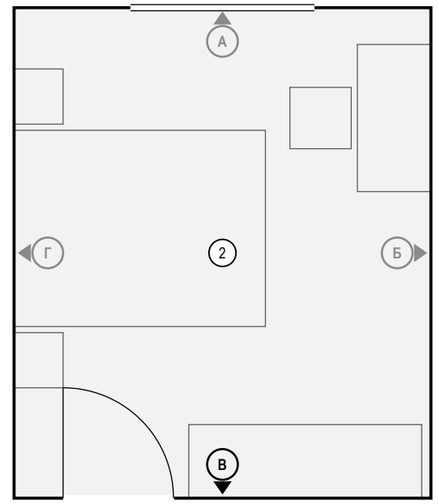


Ведомость отделки (на листе)

Марка	Поверхность	Материал, изделие	Цвет, код	Кол.
О1	стены	окраска, Tikkurila Euro Power 7, колеровка по NCS, матовая, подготовка Q3	NCS S 0804-Y30R «S 0804-Y30R»	1,8 м²
О4	плинтус	плинтус МДФ, h 80 мм, аналог: плинтус МДФ под покраску 80×16	NCS S 0804-Y30R «S 0804-Y30R»	0,6 м
О5	потолок	окраска, Tikkurila Euro Power 7, глубокоматовая, подготовка Q3	Tikkurila F485 «Damask»	13,6 м²

Ведомость изделий и проёмов (на листе)

Марка	Изделие, проём	На виде Ш×В, мм	Низ, мм
М-19	шкаф распашной 1900×600 до 2400, фасады — дуб рифлёный	1900×2400	0
Д-3	дверь скрытого монтажа	900×2100	0

2 **Стык покрытий пола Т-профилем без перепада (М 1:5)**
Узел 2 — лист С12

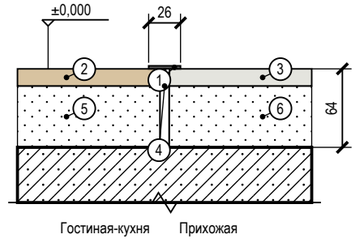

Поз.	Состав слоя, изделие
1	Т-профиль алюминиевый, полка 26 мм, ножка в шов; цвет — по покрытию
2	Гостиная-кухня: инженерная доска на клею
3	Прихожая: керамогранит на клею С2 TE S1
4	шов 8 мм по оси полотна двери, заполнитель эластичный
5	Гостиная-кухня: стяжка ЦПС М200 50 мм
6	Прихожая: стяжка ЦПС М200 50 мм

Примечания

1. Размеры — в мм от чистовых поверхностей стен; условные обозначения и общие указания — лист 10.
2. Двери скрытого монтажа — полотно в плоскости стены, отделка стены по полотну, плинтус прерывается у короба (узел — на листе узлов).
3. Потолок — у каждой стены свой, по плану потолков (ПТ1); ступени — зоной, кромка короба перед нишей — тонкой линией; в поле потолка: ПТ2 +2,600.

	Лист	№ док.	Подпись	Дата
Дизайнер	Кырлан А.С.			13.11.26
Проверил				
Н. контр.				
Утв.				


Проект: Квартира 56 м² — **М 1:20**

Развёртка стены В. Спальня (пом. 2)

Стадия	Лист	Листов
П	60	92

выпуск 13.11.2026 № 568a382a0d · стр. 60 из 92


Стена Г (М 1:20)

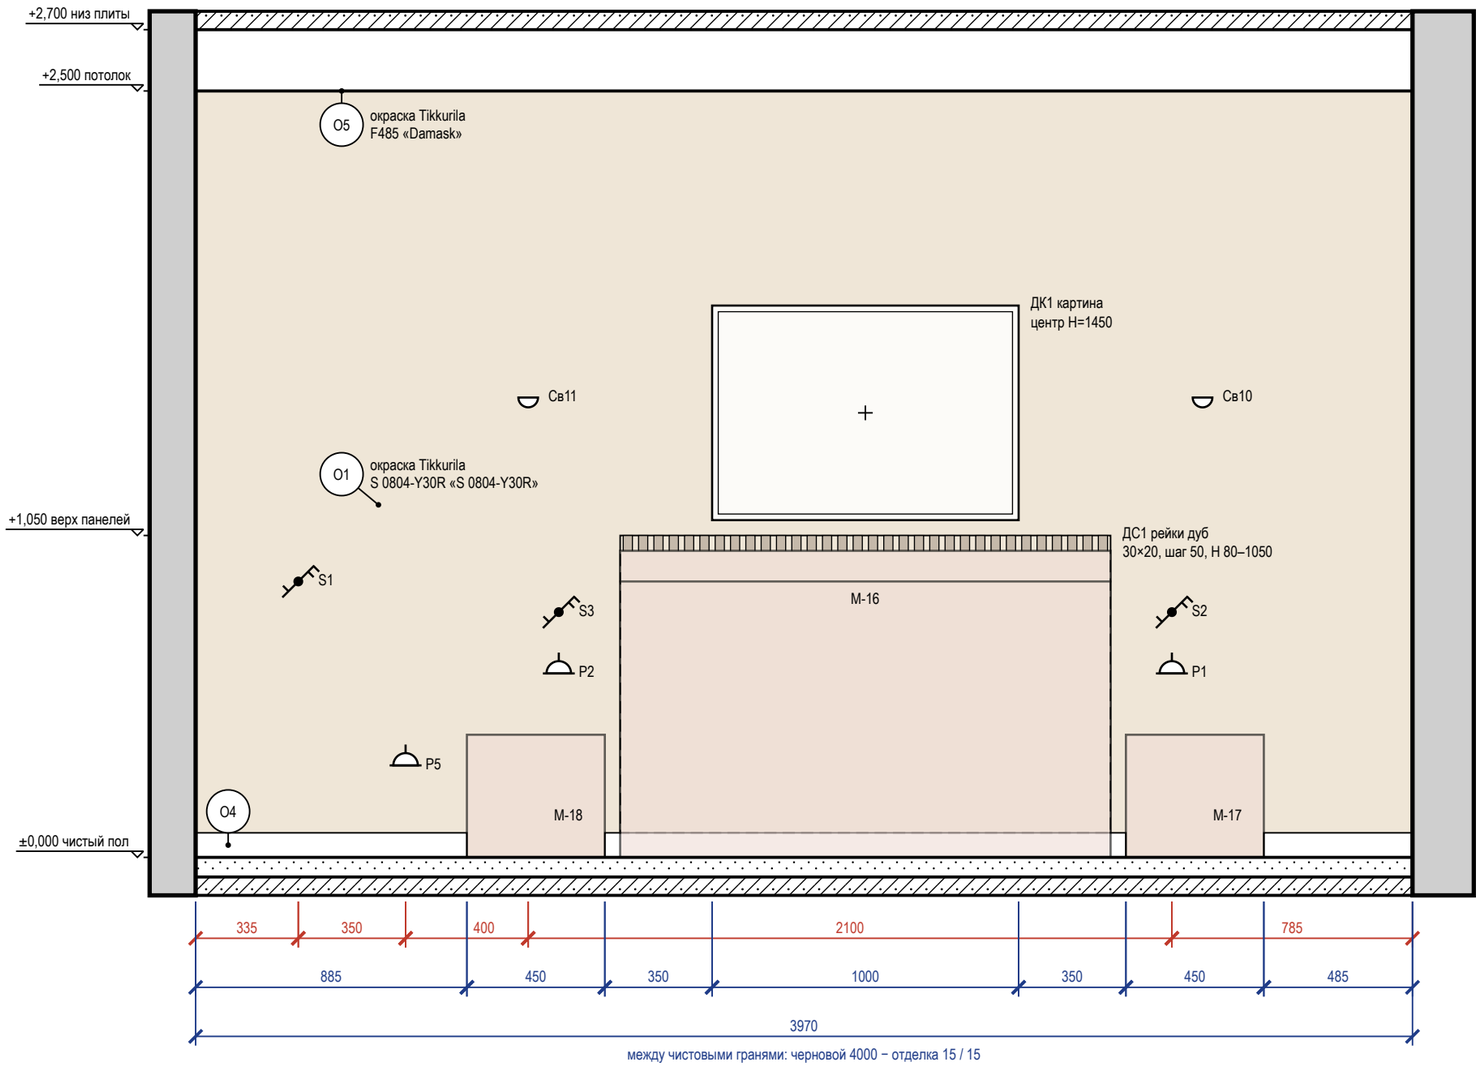

Ведомость отделки (на листе)

Марка	Поверхность	Материал, изделие	Цвет, код	Кол.
О1	стены	окраска, Tikkurila Euro Power 7, колеровка по NCS, матовая, подготовка Q3	NCS S 0804-Y30R «S 0804-Y30R»	9,9 м²
О4	плинтус	плинтус МДФ, h 80 мм, аналог: плинтус МДФ под покраску 80×16	NCS S 0804-Y30R «S 0804-Y30R»	3,1 м
О5	потолок	окраска, Tikkurila Euro Power 7, глубокоматовая, подготовка Q3	Tikkurila F485 «Damask»	13,6 м²
ДС1	рейки	рейки, дуб, 30×20 мм, шаг 50 мм, аналог: рейка массив дуба 30×20, шлифованная, под масло, масло с пигментом, колеровка в тон V484 Driftwood	Tikkurila V484 «Driftwood»	1,6 м²

Схема развёрток (М 1:50)

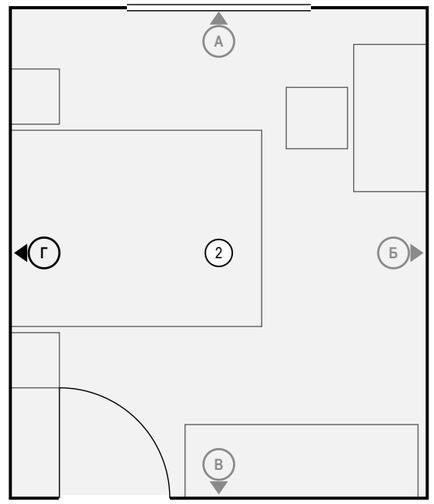

Ведомость точек и выводов

Марка	Что это	Гр.	H, мм	От угла, мм	Примечание
S1	выключатель	1	900	335	
P5	розетка: торшер	4	300	685	
Св11	светильник настенный	1	1500	1085	
P2	розетка: у кровати	4	600	1185	

Марка	Что это	Гр.	H, мм	От угла, мм	Примечание
S3	выключатель	1	800	1185	
P1	розетка: у кровати	4	600	3185	
S2	выключатель	1	800	3185	
Св10	светильник настенный	1	1500	3285	

Ведомость изделий и проёмов (на листе)

Марка	Изделие, проём	На виде Ш×В, мм	Низ, мм
М-18	тумба прикроватная, дуб	450×400	0
М-16	кровать-подиум 1600×2000, дуб, изголовье 900	1600×900	0
ДК1	картина	1000×700	1100
М-17	тумба прикроватная, дуб	450×400	0

Примечания

1. Размеры — в мм от чистовых поверхностей стен; условные обозначения и общие указания — лист 10.
2. Картины и зеркала крепить к основанию по паспорту изделия (закладные и анкеры — в перечне скрытых работ); крест — ось центра предмета.
3. Объёмная отделка стен — по ведомости отделки листа: материал, сечение, шаг и отметки — по подписи у элемента; рейки и рамки молдингов раскладываются от середины поля; крепление — по паспорту изделия.
4. Потолок — у каждой стены свой, по плану потолков (ПТ1); ступени — зоной, кромка короба перед нишей — тонкой линией; в поле потолка: ПТ2 +2,600.

	Лист	№ док.	Подпись	Дата
Дизайнер	Кырлан А.С.			13.11.26
Проверил				
Н. контр.				
Утв.				


Проект: Квартира 56 м² — **М 1:20**

Развёртка стены Г. Спальня (пом. 2)

Стадия	Лист	Листов
П	61	92


выпуск 13.11.2026 № 568a382a0d · стр. 61 из 92

Стена А (М 1:25)

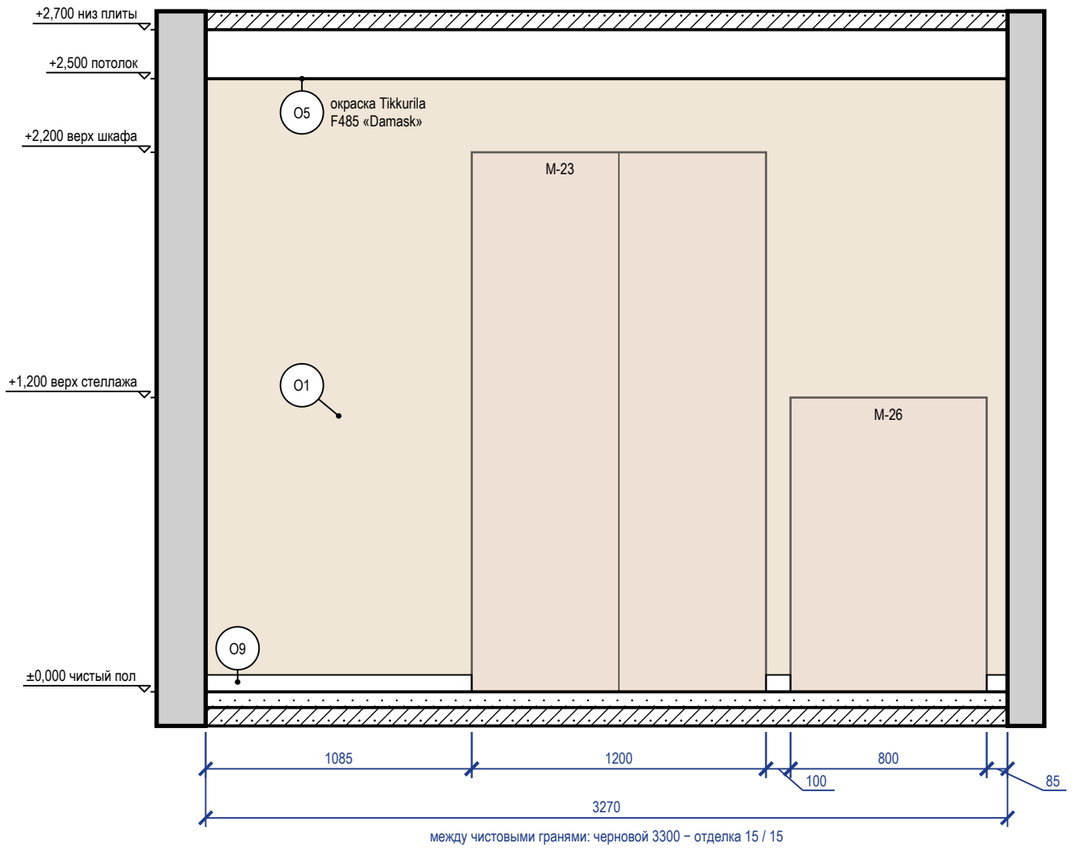

между чистовыми гранями: черновой 3300 − отделка 15 / 15

Стена Б (М 1:25)

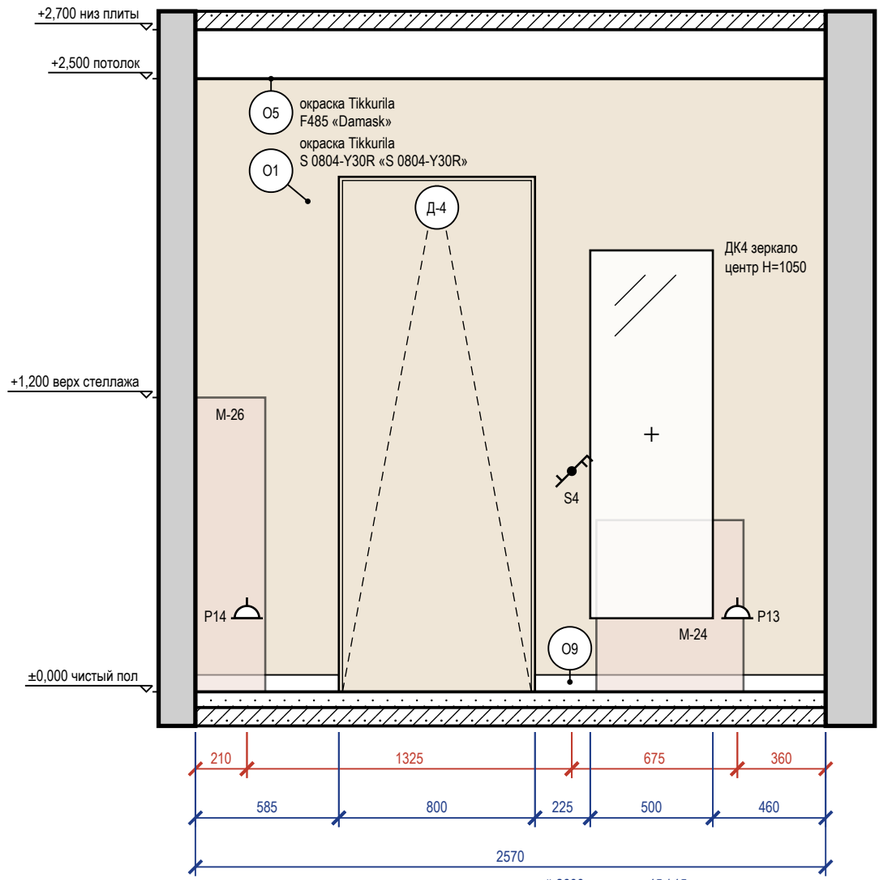


между чистовыми гранями: черновой 2600 − отделка 15 / 15


Ведомость точек и выводов

Стена	Марка	Что это	Гр.	Н, мм	От угла, мм	Примечание
Б	Р14	розетка: уборка у входа	5	300	210	
Б	S4	выключатель	1	900	1535	
Б	Р13	розетка: уборка	5	300	2210	


Схема развёрток (М 1:100)

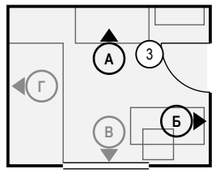

Стена А — визуализация, лист 6

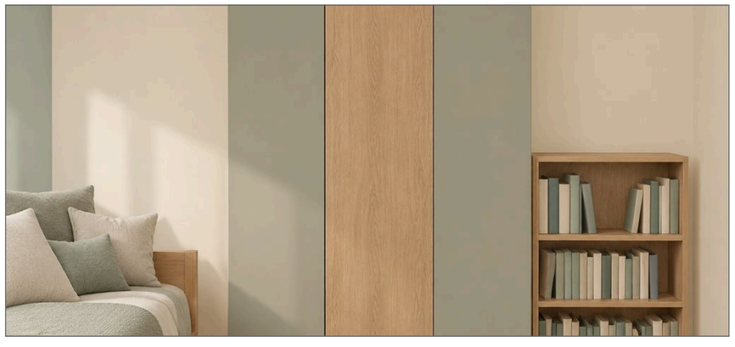

Стена Б — визуализация, лист 7

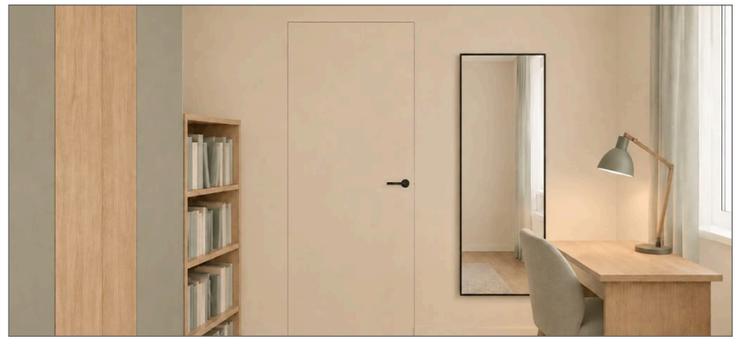


Примечания

1. Размеры — в мм от чистовых поверхностей стен; условные обозначения и общие указания — лист 10.
2. Отделка стен — по ведомости отделки помещений, лист С1.
3. Картины и зеркала крепить к основанию по паспорту изделия (закладные и анкеры — в перечне скрытых работ); крест — ось центра предмета.
4. Двери скрытого монтажа — полотно в плоскости стены, отделка стены по полотну, плинтус прерывается у короба (узел — на листе узлов).
5. Потолок — у каждой стены свой, по плану потолков (ПТ1); ступени — зоной, кромка короба перед нишей — тонкой линией; в поле потолка: ПТ2 +2,600.

	Лист	№ док.	Подпись	Дата	Проект: Квартира 56 м²	М 1:25		
Дизайнер	Кырлан А.С.			13.11.26				
Проверил					Развёртки стен А, Б. Детская (пом. 3)	Стадия	Лист	Листов
Н. контр.								
Утв.						П	62	92


выпуск 13.11.2026 № 568a382a0d · стр. 62 из 92

Стена В (М 1:25)

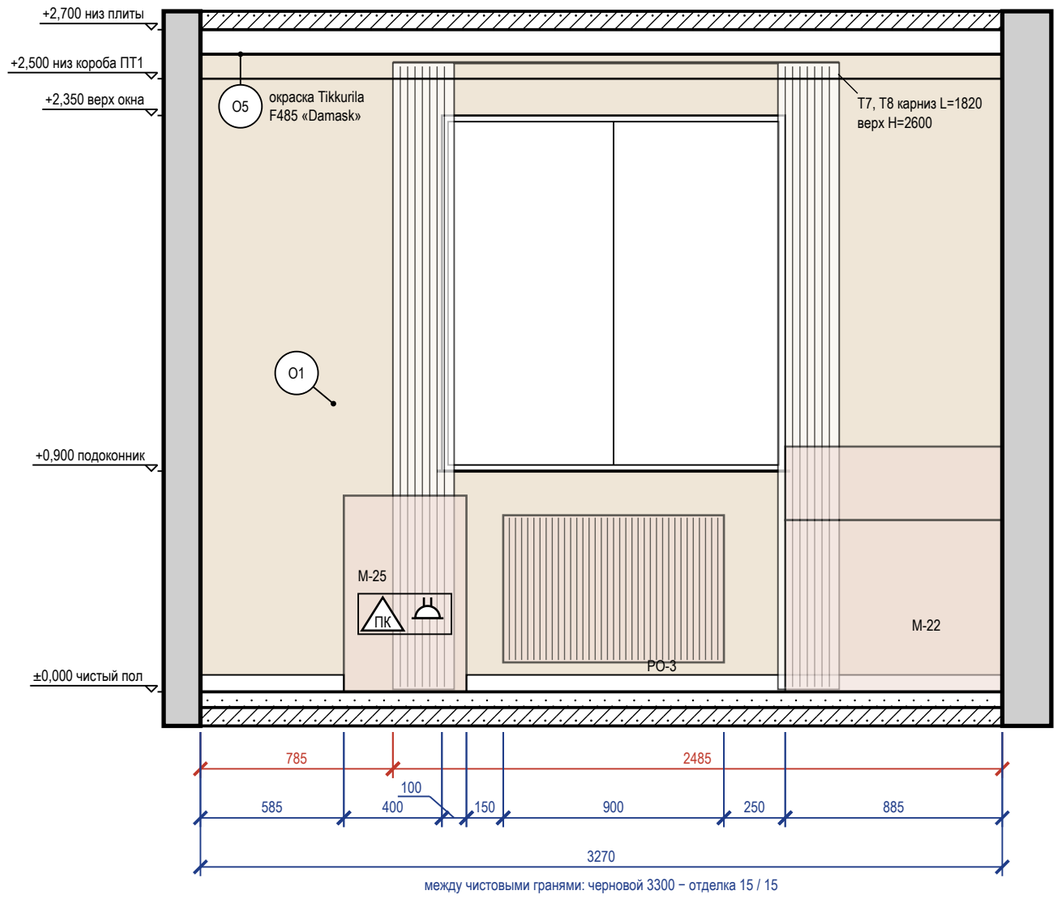

между чистовыми гранями: черновой 3300 − отделка 15 / 15

Стена Г (М 1:25)

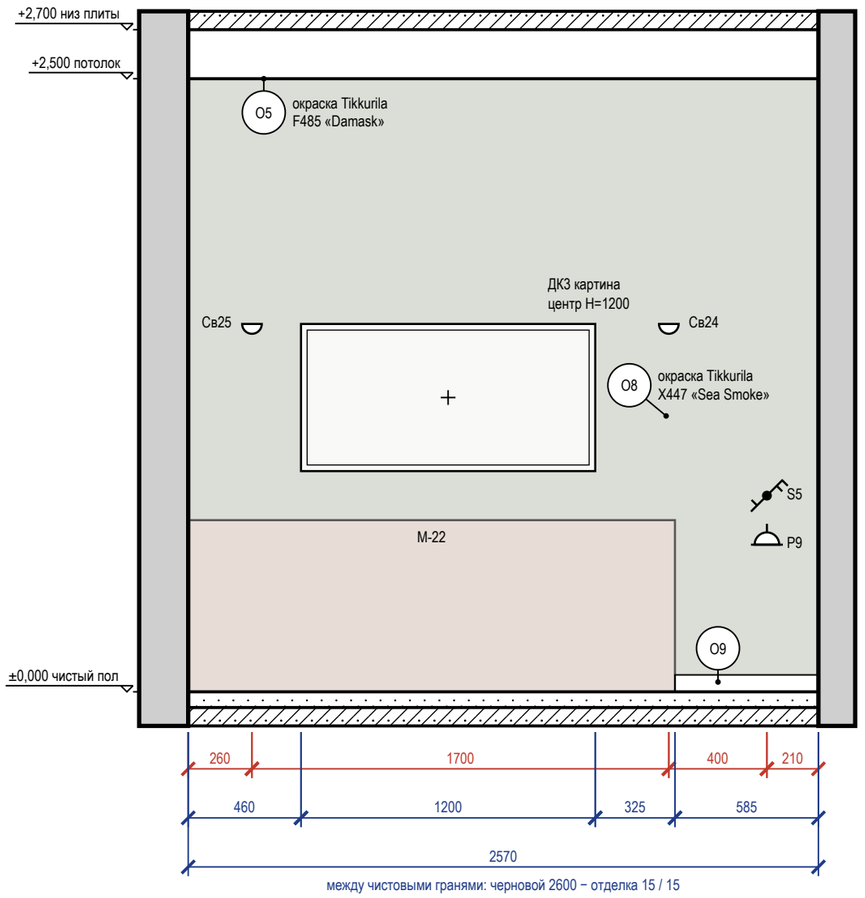

между чистовыми гранями: черновой 2600 − отделка 15 / 15


Ведомость точек и выводов

Стена	Марка	Что это	Гр.	H, мм	От угла, мм	Примечание
В	LAN2	розетка RJ45: рабочий стол		300	785	
В	P11	розетка: рабочий стол	5	300	885	рамка 2 поста
Г	Св25	светильник настенный	1	1500	260	
Г	Св24	светильник настенный	1	1500	1960	
Г	P9	розетка: у кровати	5	600	2360	
Г	S5	выключатель	1	800	2360	

Ведомость отделки (на листе)

Марка	Поверхность	Материал, изделие	Цвет, код	Кол.
О1	стены	окраска, Tikkurila Euro Power 7, колеровка по NCS, матовая, подготовка Q3	NCS S 0804-Y30R «S 0804-Y30R»	6,5 м²
О5	потолок	окраска, Tikkurila Euro Power 7, глубокоматовая, подготовка Q3	Tikkurila F485 «Damask»	8,6 м²
О8	акцентная стена	окраска, Tikkurila Euro Power 7, матовая, подготовка Q3	Tikkurila X447 «Sea Smoke»	6,4 м²
О9	плинтус	плинтус МДФ, Orac Decor Contour (Luxxus), h 69 мм, SX165	NCS S 0804-Y30R «S 0804-Y30R»	3,4 м

Схема развёрток (М 1:50)

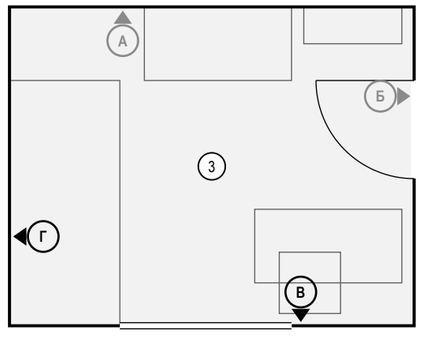


Примечания

1. Размеры — в мм от чистовых поверхностей стен; условные обозначения и общие указания — лист 10.
2. Картины и зеркала крепить к основанию по паспорту изделия (закладные и анкеры — в перечне скрытых работ); крест — ось центра предмета.
3. Карнизы (шины) — по ведомости текстиля декоратора: длина L и верх H на развёртке — те же числа, что в ведомости; крепление — до окраски потолка.
4. Потолок — у каждой стены свой, по плану потолков (НШ2, ПТ1); ступени — зоной, кромка короба перед нишей — тонкой линией; в поле потолка: ПТ2 +2,600.
5. Линии узора (швы плитки, складки штор, рёбра радиаторов) прерываются у знаков и выносок — просвет между линиями не менее 0,7 мм.
6. Часть марок не уместилась у знаков: коды, высоты и привязки этих позиций — в ведомости точек и выводов под видами.

	Лист	№ док.	Подпись	Дата	Проект: Квартира 56 м²	М 1:25		
Дизайнер	Кырлан А.С.			13.11.26				
Проверил					Развёртки стен В, Г. Детская (пом. 3)	Стадия	Лист	Листов
Н. контр.						П	63	92
Утв.								


выпуск 13.11.2026 № 568a382a0d · стр. 63 из 92

Стена А (М 1:25)

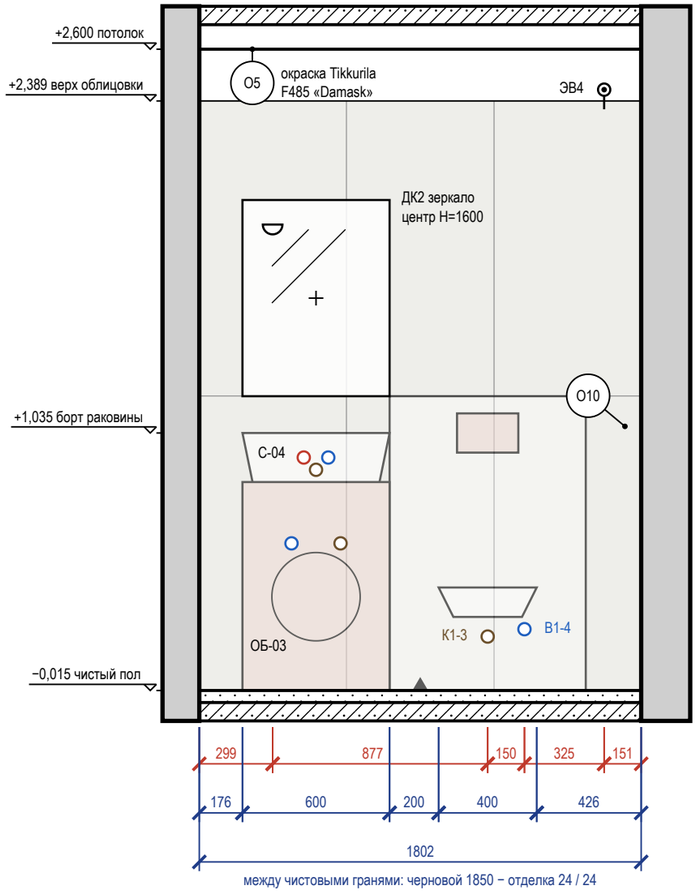

между чистовыми гранями: черновой 1850 − отделка 24 / 24

Стена Б (М 1:25)

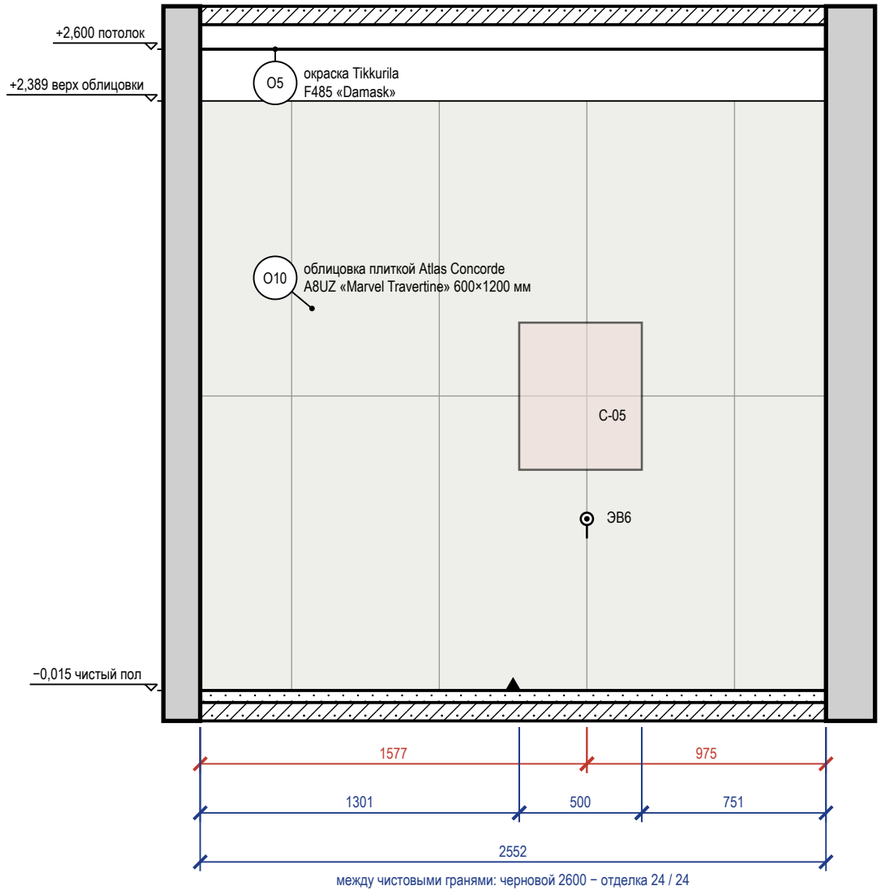


между чистовыми гранями: черновой 2600 − отделка 24 / 24

Стена А — визуализация, лист 8



Схема развёрток (М 1:50)

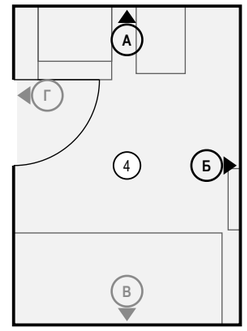

Ведомость точек и выводов

Стена	Марка	Что это	Гр.	Н, мм	От угла, мм	Примечание
А	Св15	светильник настенный	3	1900	299	
А	В1-6	холодная вода — стиральная машина		600	376	кран машины
А	Т3-3	горячая вода — умывальник		950	426	межос. 100
А	К1-4	канализация — умывальник		900	476	Ø50; плоский сифон, над машиной
А	В1-5	холодная вода — умывальник		950	526	межос. 100
А	К1-5	канализация — стиральная машина		600	576	Ø50
А	К1-3	канализация — унитаз подвесной		220	1176	Ø110
А	В1-4	холодная вода — унитаз подвесной		250	1326	в раме инсталляции
А	ЭВ4	вывод кабеля: вентилятор ВР1 (таймер выбега)	3	2450	1651	
Б	ЭВ6	вывод кабеля: полотенцесушитель С-05	13	700	1577	

Ведомость отделки (на листе)

Марка	Поверхность	Материал, изделие	Цвет, код	Кол.
О5	потолок	окраска, Tikkurila Euro Power 7, матовая, подготовка Q3	Tikkurila F485 «Damask»	4,8 м²
О10	стены	облицовка плиткой, Atlas Concorde Marvel Travertine, 600×1200×9 мм, A8UZ, затирка CG2WA	Atlas Concorde A8UZ «Marvel Travertine»	10,5 м²

Примечания

1. Размеры — в мм от чистовых поверхностей стен; условные обозначения и общие указания — лист 10.
2. Схема мебели, приборов и декора не является технической документацией для производства мебели; габариты — по паспортам изделий.
3. Выводы ВК — коды и высоты по листу выводов сантехники.
4. Облицовка — по сетке швов 2 мм, раскладка от оси стены (треугольник у пола), целые ряды от пола; подрезки — по листу раскладки плитки.
5. Гидроизоляция в 2 слоя, заход на стены 200 мм; над ванной — до 2000 и 300 мм за борт — до облицовки, с актом скрытых работ и тестом проливом (узел — на листе узлов).
6. Картины и зеркала крепить к основанию по паспорту изделия (закладные и анкеры — в перечне скрытых работ); крест — ось центра предмета.
7. Часть марок не уместилась у знаков: коды, высоты и привязки этих позиций — в ведомости точек и выводов под видами.

	Лист	№ док.	Подпись	Дата
Дизайнер	Кырлан А.С.			13.11.26
Проверил				
Н. контр.				
Утв.				


Проект: Квартира 56 м² — **М 1:25**

Развёртки стен А, Б. Санузел (пом. 4)

Стадия	Лист	Листов
П	64	92


выпуск 13.11.2026 № 568a382a0d · стр. 64 из 92

Стена В (М 1:25)

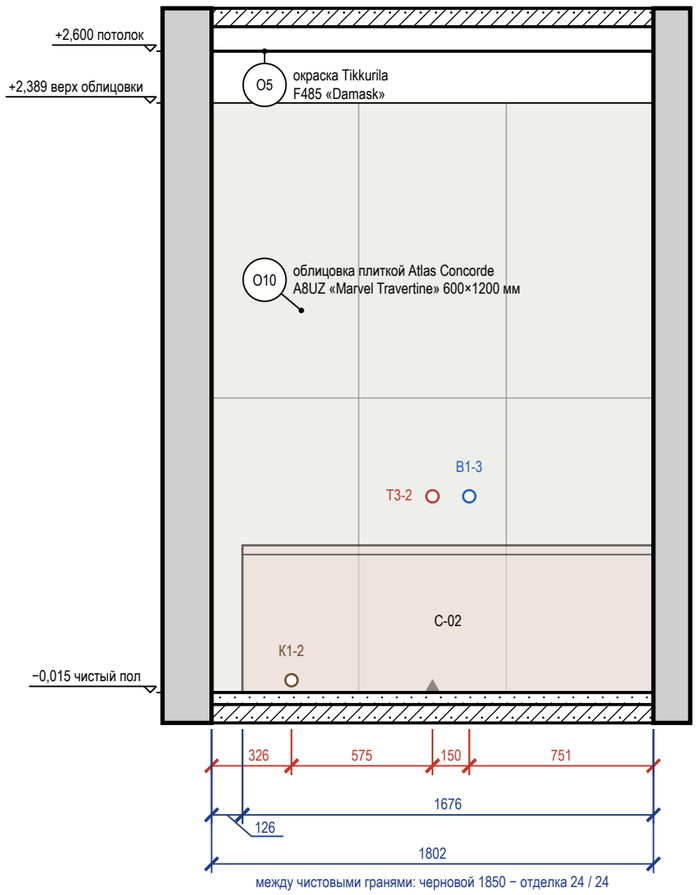


между чистовыми гранями: черновой 1850 − отделка 24 / 24

Стена Г (М 1:25)

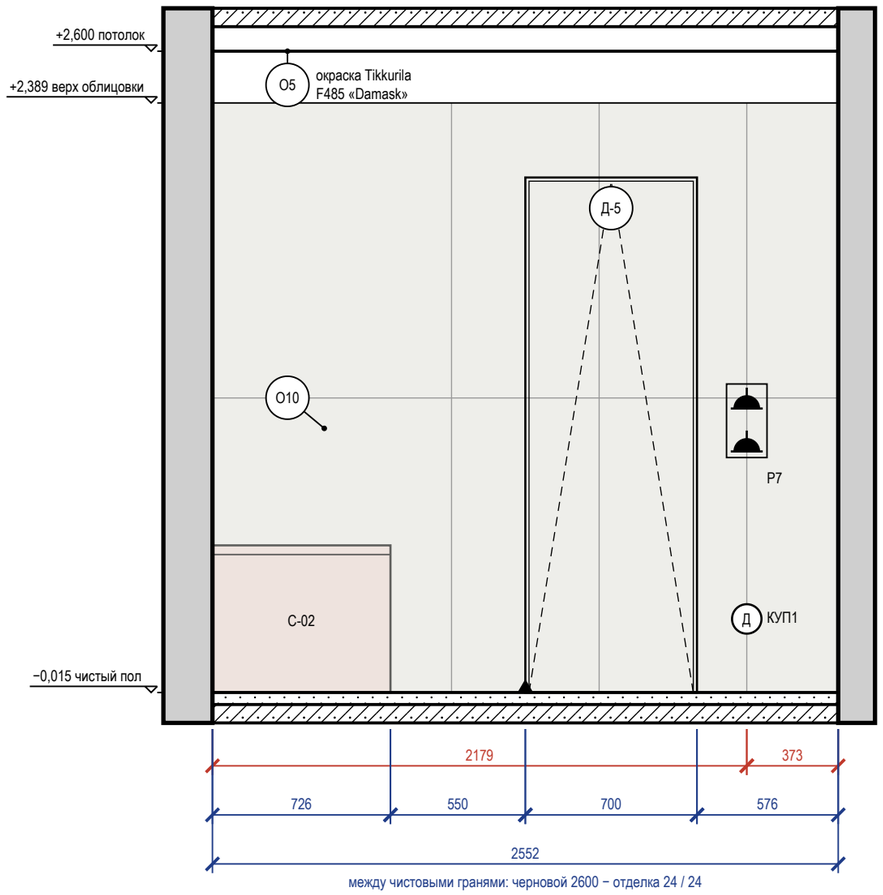

между чистовыми гранями: черновой 2600 − отделка 24 / 24

Схема развёрток (М 1:50)

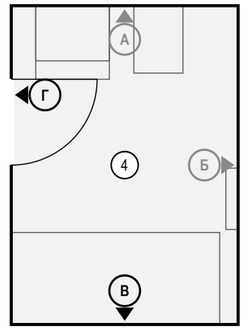


Ведомость изделий и проёмов (на листе)

Стена	Марка	Изделие, проём	На виде Ш×В, мм	Низ, мм
В	С-02	ванна 1700×750 акриловая, экран под плитку	1676×600	0
Г	С-02	ванна 1700×750 акриловая, экран под плитку	726×600	0
Г	Д-5	дверь скрытого монтажа	700×2100	0

Ведомость точек и выводов

Стена	Марка	Что это	Гр.	Н, мм	От угла, мм	Примечание
В	К1-2	канализация — ванна		50	326	Ø50
В	Т3-2	горячая вода — ванна		800	901	межос. 150
В	В1-3	холодная вода — ванна		800	1051	межос. 150
Г	КУП1	КУП (уравнивание потенциалов): КУП уравнивание потенциалов (ДСУП)		300	2179	
Г	Р7	розетка: стиральная машина	12	1000	2179	IP44
Г	Р8	розетка: фен у умывальника	13	1141	2179	IP44

Стена Г — визуализация, лист 9

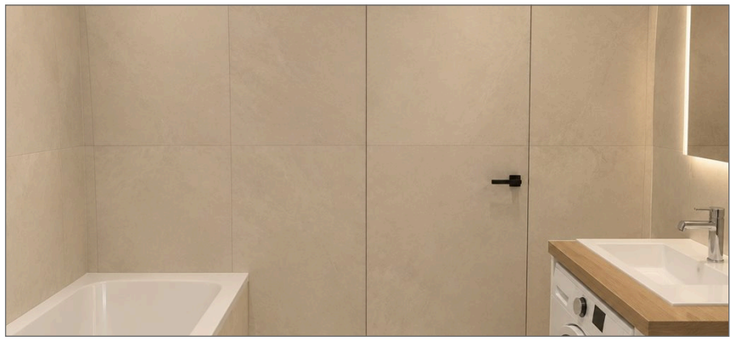

Ведомость отделки (на листе)

Марка	Поверхность	Материал, изделие	Цвет, код	Кол.
О5	потолок	окраска, Tikkurila Euro Power 7, матовая, подготовка Q3	Tikkurila F485 «Damask»	4,8 м²
О10	стены	облицовка плиткой, Atlas Concorde Marvel Travertine, 600×1200×9 мм, A8UZ, затирка CG2WA	Atlas Concorde A8UZ «Marvel Travertine»	9 м²


Примечания

1. Размеры — в мм от чистовых поверхностей стен; условные обозначения и общие указания — лист 10.
2. Схема мебели, приборов и декора не является технической документацией для производства мебели; габариты — по паспортам изделий.
3. Выводы ВК — коды и высоты по листу выводов сантехники.
4. Облицовка — по сетке швов 2 мм, раскладка от оси стены (треугольник у пола), целые ряды от пола; подрезки — по листу раскладки плитки.
5. Гидроизоляция в 2 слоя, заход на стены 200 мм; над ванной — до 2000 и 300 мм за борт — до облицовки, с актом скрытых работ и тестом проливом (узел — на листе узлов).
6. Двери скрытого монтажа — полотно в плоскости стены, отделка стены по полотну, плинтус прерывается у короба (узел — на листе узлов).
7. Часть марок не уместилась у знаков: коды, высоты и привязки этих позиций — в ведомости точек и выводов под видами.

	Лист	№ док.	Подпись	Дата	Проект: Квартира 56 м²	М 1:25		
Дизайнер	Кырлан А.С.			13.11.26				
Проверил					Развёртки стен В, Г. Санузел (пом. 4)	Стадия	Лист	Листов
Н. контр.						П	65	92
Утв.								


выпуск 13.11.2026 № 568a382a0d · стр. 65 из 92

Стена А (М 1:25)

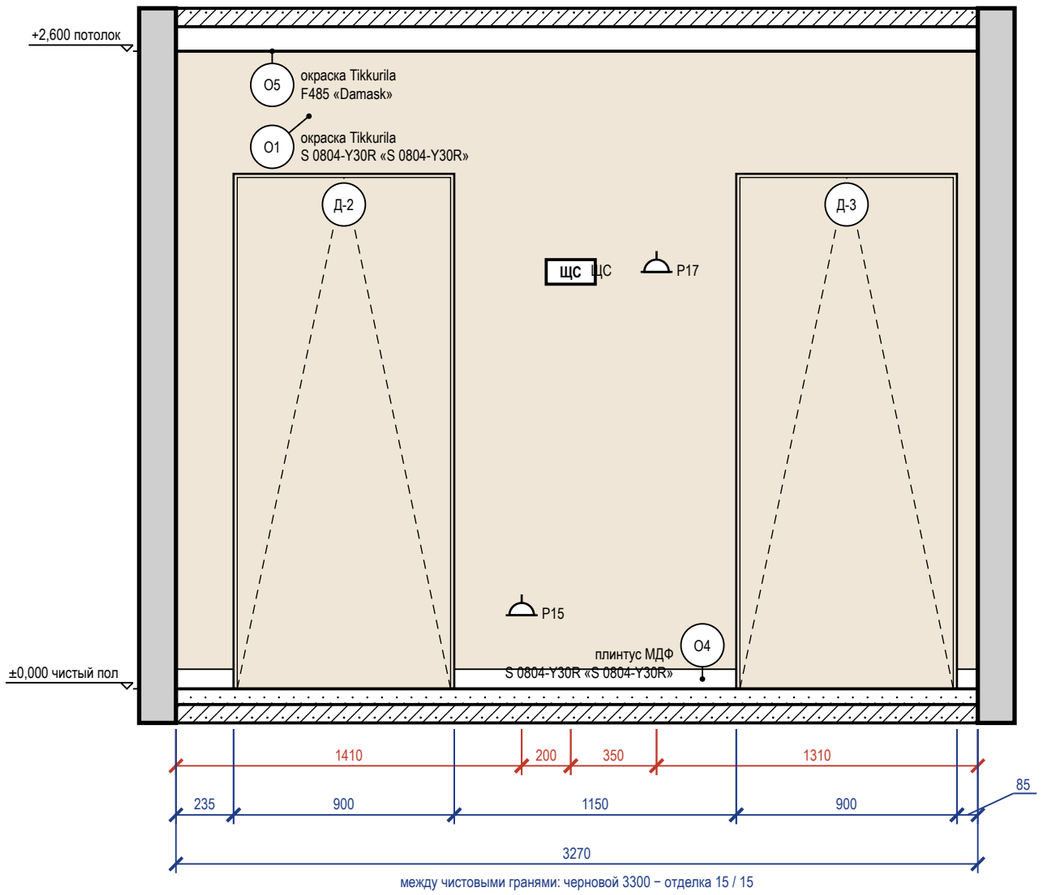

между чистовыми гранями: черновой 3300 − отделка 15 / 15

Стена Б (М 1:25)

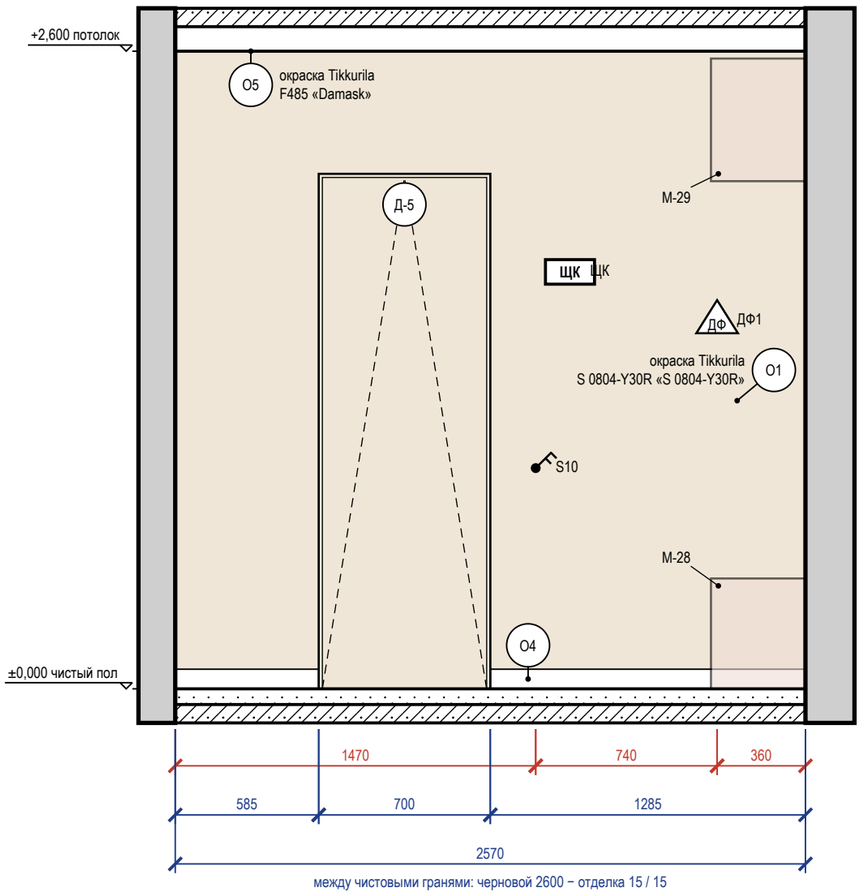

между чистовыми гранями: черновой 2600 − отделка 15 / 15


Ведомость точек и выводов

Стена	Марка	Что это	Гр.	Н, мм	От угла, мм	Примечание
А	Р15	розетка: пылесос, сушилка обуви	6	300	1410	
А	ЩС	щит: щит слаботочный: ввод оптики, ONT, роутер, патч-панель		1700	1610	
А	Р17	розетка: питание слаботочного щита (рядом с ЩС)	14	1700	1960	
Б	S10	выключатель	3	900	1470	
Б	ЩК	щит: щит квартирный ЩРВ-П-48		1700	1610	
Б	ДФ1	домофон: трубка домофона		1500	2210	

Ведомость отделки (на листе)

Марка	Поверхность	Материал, изделие	Цвет, код	Кол.
О1	стены	окраска, Tikkurila Euro Power 7, колеровка по NCS, матовая, подготовка Q3	NCS S 0804-Y30R «S 0804-Y30R»	9,9 м²
О4	плинтус	плинтус МДФ, h 80 мм, аналог: плинтус МДФ под покраску 80×16	NCS S 0804-Y30R «S 0804-Y30R»	3,3 м
О5	потолок	окраска, Tikkurila Euro Power 7, глубокоматовая, подготовка Q3	Tikkurila F485 «Damask»	8,6 м²

Схема развёрток (М 1:50)

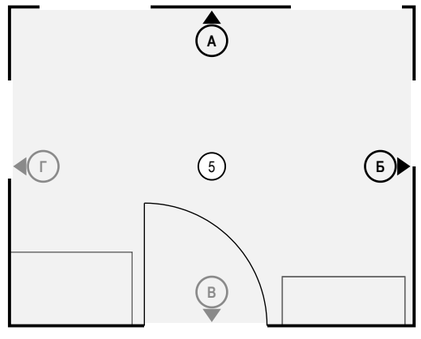


Примечания

1. Размеры — в мм от чистовых поверхностей стен; условные обозначения и общие указания — лист 10.
2. Двери скрытого монтажа — полотно в плоскости стены, отделка стены по полотну, плинтус прерывается у короба (узел — на листе узлов).


	Лист	№ док.	Подпись	Дата	Проект: Квартира 56 м²	М 1:25		
Дизайнер	Кырлан А.С.			13.11.26	Развёртки стен А, Б. Прихожая (пом. 5)	Стадия	Лист	Листов
Проверил						П	66	92
Н. контр.								
Утв.								

Стена В (М 1:25)

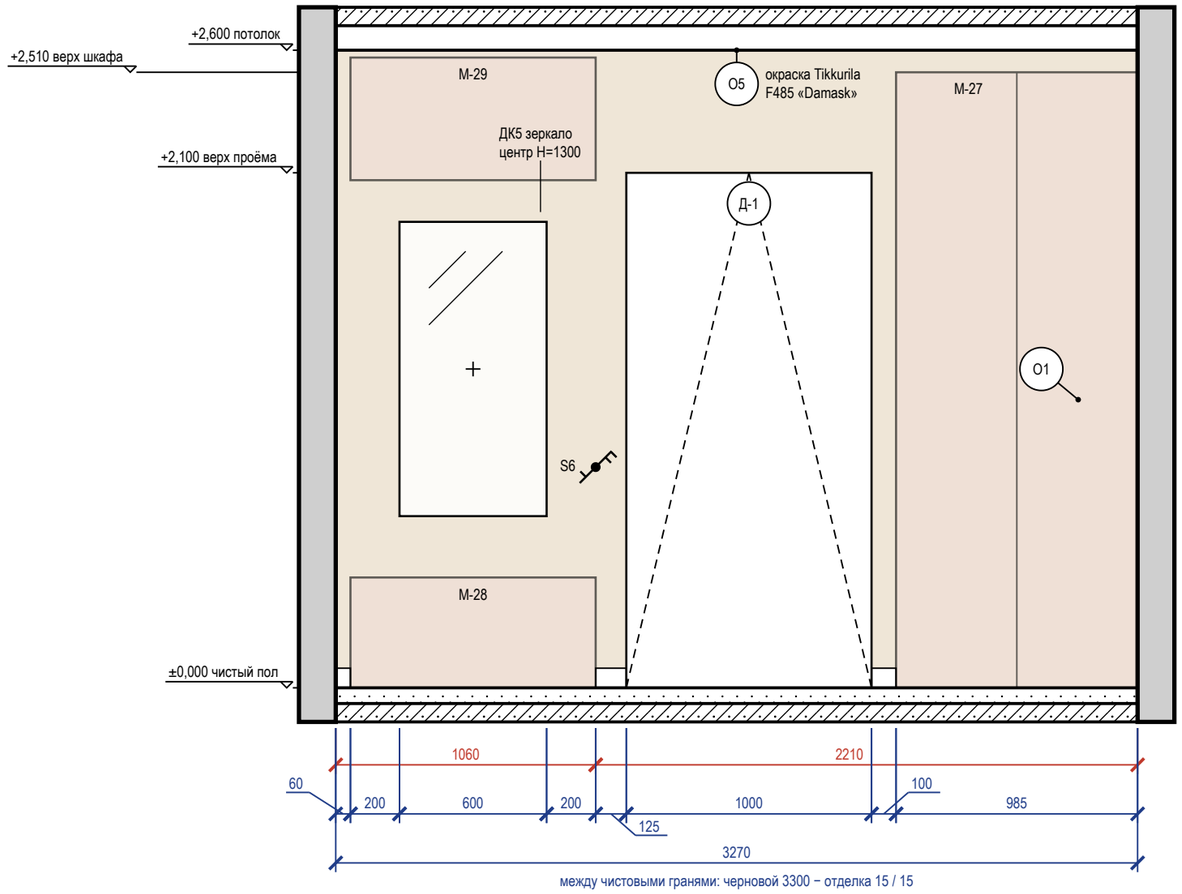

между чистовыми гранями: черновой 3300 − отделка 15 / 15

Стена Г (М 1:25)

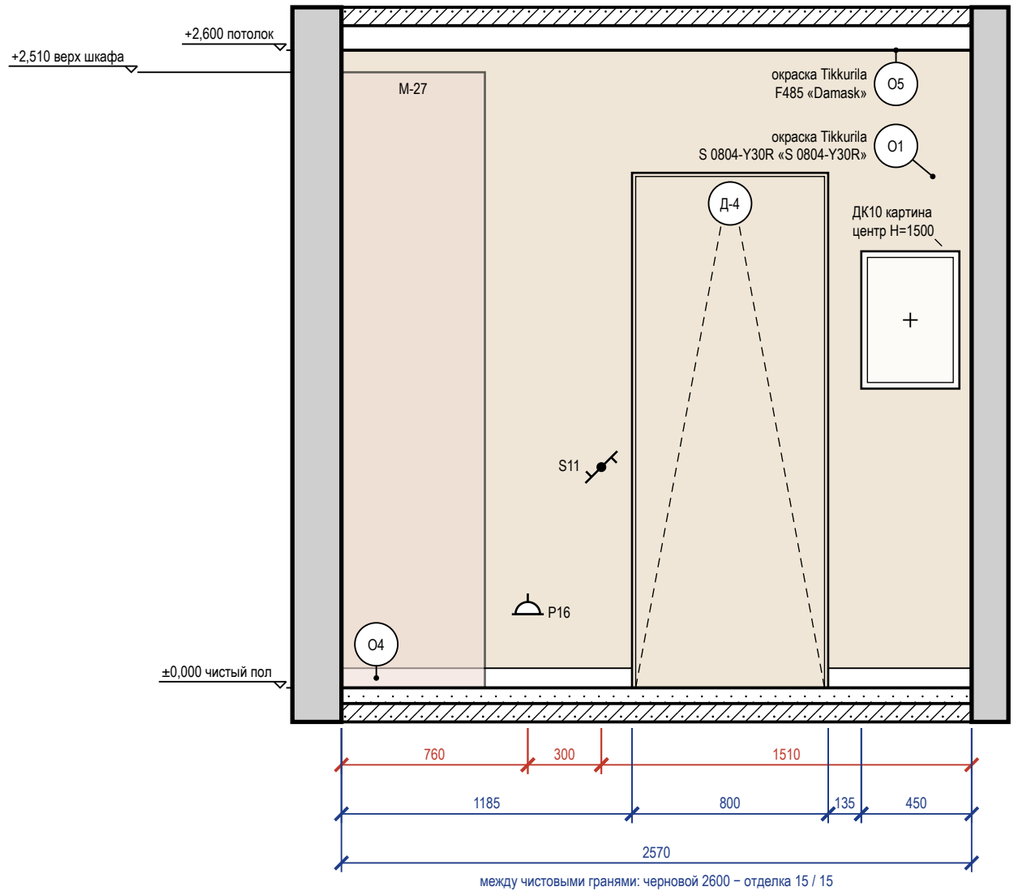

между чистовыми гранями: черновой 2600 − отделка 15 / 15


Ведомость точек и выводов

Стена	Марка	Что это	Гр.	H, мм	От угла, мм	Примечание
В	S6	выключатель	2	900	1060	
Г	P16	розетка: уборка	6	300	760	
Г	S11	выключатель	2	900	1060	

Ведомость отделки (на листе)

Марка	Поверхность	Материал, изделие	Цвет, код	Кол.
О1	стены	окраска, Tikkurila Euro Power 7, колеровка по NCS, матовая, подготовка Q3	NCS S 0804-Y30R «S 0804-Y30R»	8,8 м²
О4	плинтус	плинтус МДФ, h 80 мм, аналог: плинтус МДФ под покраску 80×16	NCS S 0804-Y30R «S 0804-Y30R»	2,1 м
О5	потолок	окраска, Tikkurila Euro Power 7, глубокоматовая, подготовка Q3	Tikkurila F485 «Damask»	8,6 м²

Схема развёрток (М 1:50)

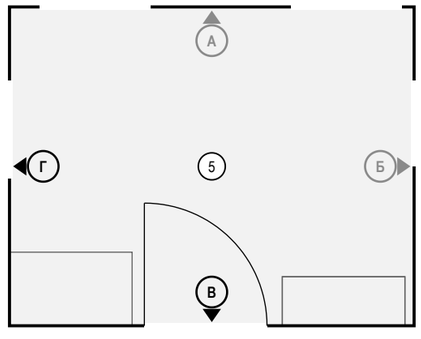

Примечания

1. Размеры — в мм от чистовых поверхностей стен; условные обозначения и общие указания — лист 10.
2. Картины и зеркала крепить к основанию по паспорту изделия (закладные и анкеры — в перечне скрытых работ); крест — ось центра предмета.
3. Двери скрытого монтажа — полотно в плоскости стены, отделка стены по полотну, плинтус прерывается у короба (узел — на листе узлов).

	Лист	№ док.	Подпись	Дата	Проект: Квартира 56 м²	М 1:25
Дизайнер	Кырлан А.С.			13.11.26		
Проверил					Развёртки стен В, Г. Прихожая (пом. 5)	Стадия: П; Лист: 67; Листов: 92
Н. контр.						
Утв.						

выпуск 13.11.2026 № 568a382a0d · стр. 67 из 92

Комплект предварительный по пунктам этих таблиц. Пока по пункту нет ответа или решения, показанное на указанном листе — допущение проектировщика, а не утверждённое решение.
Сводка: открытых вопросов — 12 (из них ждут факта объекта — 8: контрольного обмера, обследования или документа); изменений в реестре — 3, из них без подписи — 1.

Открытые вопросы и принятые допущения

№	Формулировка	Вид	Кто решает	Если решения нет	Лист, где это проявляется
К-1	Размеры помещений, толщины стен (наружные 200 мм, перегородки 150 мм) и положение проёмов введены заказчиком в бриф заказчика (site-brief-wizard, 01.08.2026): контрольный обмер на объекте не выполнялся, обмерного плана и плана БТИ в материалах нет; площадь по брифу 56 м², сумма помещений по чистым размерам брифа 56.37 м². От этого зависят все размеры альбома, площади, заказ материалов и изделий. Выполнить контрольный обмер.	Непонятно Ждёт: обмера	Архитектор-планировщик	все размеры альбома остаются по брифу заказчика и не считаются замеренными; заказ изделий по ним не ведётся	л. 12 — План планировки от заказчика л. 34 — План размещения дверей
К-2	Высота потолка 2700 мм указана заказчиком в брифе, на объекте не замерена. От неё зависят вертикальные размеры альбома (развёртки, шкафы, перегородки, объёмы работ). Замерить высоту на объекте.	Непонятно Ждёт: обмера	Архитектор-планировщик	вертикальные размеры альбома остаются по брифу и не считаются замеренными	л. 12 — План планировки от заказчика
К-3	Тип дома (монолитный) и толщина перекрытия 200 мм указаны заказчиком в брифе; проект дома, план БТИ и техническое заключение о несущих конструкциях не переданы. Несущие стены и допустимость демонтажа определяются только по этим документам или по обследованию.	Отсутствует Ждёт: документа, обследования	Архитектор-планировщик	все существующие стены считаются несущими; демонтаж и штробление в них не выполняются до технического заключения	л. 12 — План планировки от заказчика л. 13 — План демонтажа и монтажа перегородок
К-4	Положение и диаметры стояков (канализации, холодной воды) указаны заказчиком в брифе, не замерены; врезки, краны и счётчики не описаны. От стояков зависят трассы водопровода и канализации, привязки выводов и уклоны. Замерить на объекте.	Непонятно Ждёт: обмера	Инженер ВК (вода, канализация)	трассы и привязки выводов остаются по положению стояков из брифа и не считаются замеренными	л. 25 — План выводов сантехники л. 26 — Схема разводки водопровода и канализации
К-5	Новые перегородки заданы заказчиком в брифе положением, материалом и толщиной; конструкция (система, число слоёв, каркас, звукоизоляция, Rw) выбрана исполнителем по каталогам. Утвердить конструкцию перегородок или задать другую. Толщина по брифу и стена на плане расходятся: П-1 — 100 мм по брифу, П-3 — 120 мм по брифу, а план брифа построен со стенами 150 мм — на плане и в привязках стена 150. Решить, что верно: толщина по брифу (тогда соседние помещения шире, площади и привязки пересчитать) или 150 мм с отделкой.	Спорно Ждёт: решения	Архитектор-планировщик	конструкция перегородок остаётся по решению исполнителя со знаком «предложено»	л. 13 — План демонтажа и монтажа перегородок
К-6	Цвета названы заказчиком в брифе словами (тёплый белый, натуральное дерево, серо-зелёный). Исполнитель перевёл их в коды по веерам стиля джапанди: стены NCS S 0804-Y30R, потолки Tikkurila F485 Damask, второй план Tikkurila X447 Sea Smoke и V484 Driftwood, акценты Farrow & Ball No. 298 Bancha и NCS S 5010-G70Y (по комнатам). Выкрасы на объекте не делались. Утвердить коды по выкрасам. Матовость: в брифе в «не нравится» — «Глянец, холодный белый», поэтому стены матовые (в кухне-гостиной и прихожей — матовая моющаяся краска вместо полуматовой, класс мойки — по ведомости отделки); подтвердить вместе с кодами.	Спорно Ждёт: решения	Колорист-комплектатор	коды — предложение исполнителя; краску не закупать до выкрасов	л. 19 — Колерная карта
К-7	Планировка принята по брифу заказчика: положение существующих стен и проёмов, объединение кухни с гостиной (демонтаж С-1), расширение санузла (демонтаж С-2, перегородка П-1) введены в мастер брифа без обмерного плана и плана БТИ. Расстановка мебели и кухни, рабочее место в спальне, антресоль в прихожей — предложение исполнителя по этой планировке. Нужны план БТИ и контрольный обмер; до них планировочное решение — предварительное.	Непонятно Ждёт: документа	Архитектор-планировщик	расстановка остаётся предложением; мебель на заказ (кухня, шкафы) не заказывать	л. 12 — План планировки от заказчика л. 13 — План демонтажа и монтажа перегородок л. 20 — План размещения мебели и оборудования
К-8	Разрешённая мощность квартиры по ТУ в брифе не указана; принята 10 кВт (квартира с электроплитой, монолитный дом). Передать ТУ или справку УК.	Отсутствует Ждёт: документа	Инженер-электрик	щит и группы рассчитаны на 10 кВт; при меньших ТУ пересчёт групп варочной панели и духового шкафа	л. 40 — Однолинейная схема щита
К-9	Вентканалы в брифе не показаны: принято два канала — ВК-1 в санузле у стояков (стена А) и ВК-2 у стены В бывшей кухни. От них зависят вытяжка санузла, вытяжка над плитой (до обмера — рециркуляция) и короба потолка. Замерить положение и сечение на объекте.	Отсутствует Ждёт: обмера	Инженер ОВ	вытяжка кухни — рециркуляционная; вентилятор санузла по месту ВК-1 после обмера	л. 48 — План вентиляции л. 25 — План выводов сантехники
К-10	Климатический подрайон (СП 131.13330) не задан: принят не северный — жилые комнаты и кухня под потолком от 2,5 м (СП 54, п. 5.12); в IA, IБ, IГ, IД, IVA — от 2,7 м.	Отсутствует Ждёт: документа	Архитектор-планировщик	отметки потолков жилых — по 2,5 м; при северном подрайоне уровни ниже 2,7 м пересчитать до заказа каркаса	л. 36 — План потолков

	Лист	№ док.	Подпись	Дата	Проект: Квартира 56 м²			
Дизайнер	Кырлан А.С.			13.11.26	Открытые вопросы, принятые допущения и конфликты. Лист 1 из 2	Стадия	Лист	Листов
Проверил						П	68	92
Н. контр.								
Утв.								

выпуск 13.11.2026 № 568a382a0d · стр. 68 из 92

Открытые вопросы и принятые допущения (продолжение)

№	Формулировка	Вид	Кто решает	Если решения нет	Лист, где это проявляется
К-11	Мойка кухонная С-01 (пом. 1 «Гостиная-кухня»), выпуск К1-1 Ø50: до стояка Ст К1-1 15,58 м через пом. 5 «Прихожая», перепад 390 мм — короб 470×110 над полом через чужие помещения (их проёмы, мебель, проход) не построить. Решить: (а) насосная установка (КНС) под мойкой/прибором с напорной трубой Ø32 к стояку (по паспорту, обслуживаемый люк); (б) подиум кухонной зоны на 470 мм с трубой под ним; (в) перенос прибора ближе к стояку Ст К1-1. Решение меняет кухню (модули, цоколь, точки ЭОМ) — за автором с заказчиком.	Спорно Ждёт: решения	Инженер ВК (вода, канализация)	выпуск К1-1 и кухню в части мойки не выполнять до решения; остальное — по листам	л. 26 — Схема разводки водопровода и канализации л. 25 — План выводов сантехники
К-12	Помещение «Спальня»: выключатель основного света L1 (S1) не у входа — у двери Д-3 со стороны ручки свободного места нет (проём в 100 мм от угла, мебель у двери, чужие точки или выключатель общий с соседним помещением; расстановка мебель и двери не двигает). Варианты: (а) петли на другую сторону — ручка уходит от угла, выключатель встаёт у ручки; (б) шкаф или тумбу у двери сдвинуть на 300 мм — место освобождается; (в) беспроводной выключатель на клее у ручки (реле в подрозетнике ближней стены) — по согласованию с заказчиком; (г) оставить как есть (S1): рука дальше 350 мм от ручки.	Спорно Ждёт: решения	Инженер-электрик	выключатель L1 остаётся на месте (S1); закладные под выключатель у двери не делать до решения	л. 47 — Управление светильниками

Изменения проекта после выпуска листов (реестр изменений)


№	Дата	Лист	Было	Стало	Кто решил, подпись
ИЗ-1	30.10.2026	л. 20 — План размещения мебели и оборудования л. 34 — План размещения дверей л. 36 — План потолков л. 45 — План освещения л. 57 — Развёртка стены В. Гостиная-кухня (пом. 1)	Гостиная-кухня: вход Д-2 (стена В, 3700…4600) упирался в спинку дивана М-12, слева проход между консолью М-15 (1600…3400) и креслом М-14 — 575 мм, справа 175 мм до стены Б. Остров потолка У2 не центрирован на стол М-11 (зазор 100 / 450), подвесы — по столу. Детская: стол М-24 вплотную к стене В над радиатором РО-3, примечание «прибор в корпусе не решён».	Д-2 — петли у правого откоса, консоль М-15 — смещение 700…2500, кресло М-14 — у 2100…2850: проход от двери к кухне 975 / 825 мм. Остров У2 — вставка А340/В1910/С2210/D1340 (центр по столу), точка ленты Св41 — х 3300. Стол М-24 — у стены Б торцом к окну (х 2775…3375, у 5550…6750), стул М-25 — х 2200, у 5900; радиатор РО-3 открыт. Знак «**» у М-15, М-14, М-24 до подписи автора.	Утверждено: Кырлан А.С., 12.11.2026. Предложил: исполнитель.
ИЗ-2	10.11.2026	л. 20 — План размещения мебели и оборудования полный альбом	Стол М-24 (детская, пом. 3) стоял вплотную к дверному проёму Д-4 в стене Б: край стола у 5550 мм = край проёма.	Стол М-24 сдвинут вдоль стены Б на 250 мм от двери: у 5800…6400 мм (было 5550…6150), х 2000…3200 прежний; зазор от проёма Д-4 250 мм. Стул М-25 сдвинут вместе со столом: у 6150…6650 (было 5900…6400), х 2200 прежний; до стены С остаётся 100 мм. Розетки Р11, LAN2 у стола на стене С (смещения 2400 и 2500) не тронуты. Стол М-24 остаётся предложением проектировщика.	Утверждено: Кырлан А.С., 12.11.2026. Предложил: исполнитель.
ИЗ-3	12.11.2026	полный альбом	Разбор двух критиков по кадрам: «стерильный шоурум, жизни нет»; ванна С-02 в кадре без смесителя — в наименовании прибора смеситель не назван. Санузел без текстиля и предметов; на столах, консоли и тумбах нет ни одной вещи; в прихожей — только зеркало над скамьёй; на диване и кроватях по 5 декоративных подушек.	Ванна С-02 — «акриловая 1700×750, смеситель настенный». Санузел: банные и ручные полотенца на полотенцесушителе С-05 (Т20, Т21), коврик 800×450 у бортика ванны (Т22; вне полотна двери Д-5), ваза с сухой веткой на полке короба инсталляции (ДК9). Прихожая: графика «энсо» 400×560 в простенке стены Г (ДК10); дорожка и консоль не заданы — свободный пол в зонах открывания пяти дверей, стены заняты щитами, домофоном и выключателями. Гостиная-кухня: книги и свеча на журнальном столике (ДК11), керамика и настольная лампа на консоли М-15 (ДК12, ДК13), керамика на столешнице кухни (ДК14). Спальня: книги на тумбе М-17 (ДК15), шеффлера в углу у окна (ДК16), рабочая лампа на столе М-20 (ДК17). Детская: рабочая лампа на столе М-24 (ДК18). Декоративных подушек — по 4 на диван и кровати (Т17, Т4, Т10: 3 → 2). Цвета — из палитры джапанди проекта: олива Bancha и S 5010-G70Y, песочный S 2005-Y30R, тёплый белый Damask. Знак «**» у позиций до подписи автора.	Не утверждено: подписи нет. решение исполнителя; предложение проектировщика, на утверждение А. С. Кырлана

Примечания


1. Номера листов — по ведомости рабочих чертежей комплекта (лист «Общие данные»).
2. Графа «Если решения нет» показывает состояние решения на листах; влияние на сроки и стоимость по пунктам не оценивалось.
3. Пункт, по которому принято решение, при следующем выпуске комплекта из таблиц исключается.

	Лист	№ док.	Подпись	Дата	Проект: Квартира 56 м²			
Дизайнер	Кырлан А.С.			13.11.26	Открытые вопросы, принятые допущения и конфликты. Лист 2 из 2	Стадия	Лист	Листов
Проверил						П	69	92
Н. контр.								
Утв.								


Вид с фасадами (М 1:20)

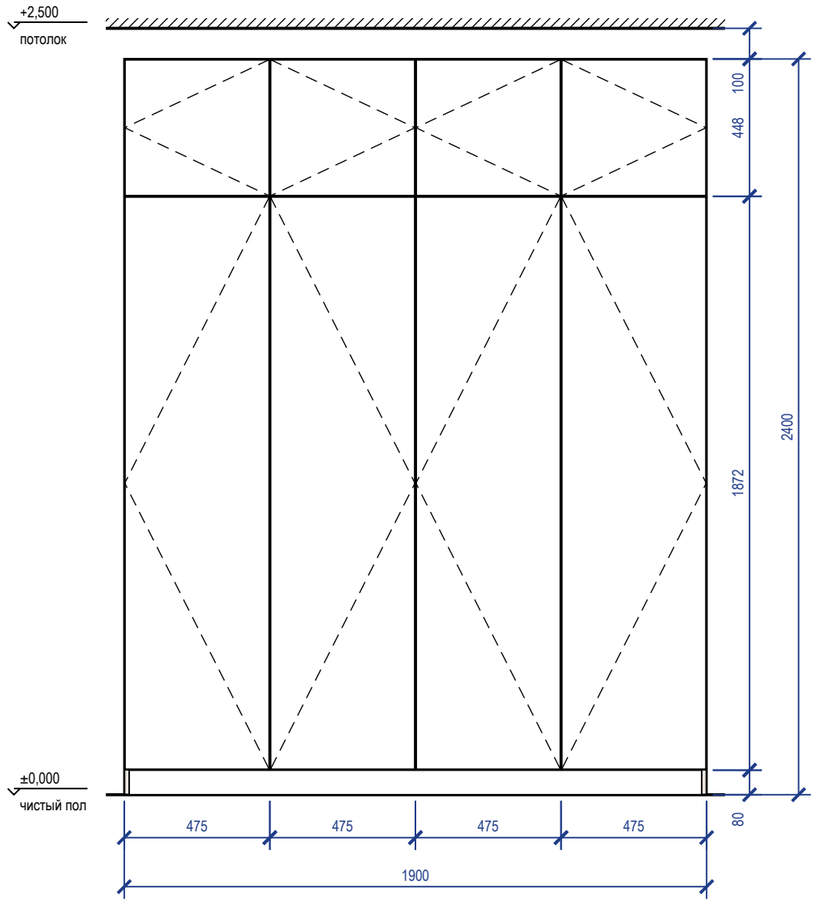


Вид без фасадов (М 1:20)

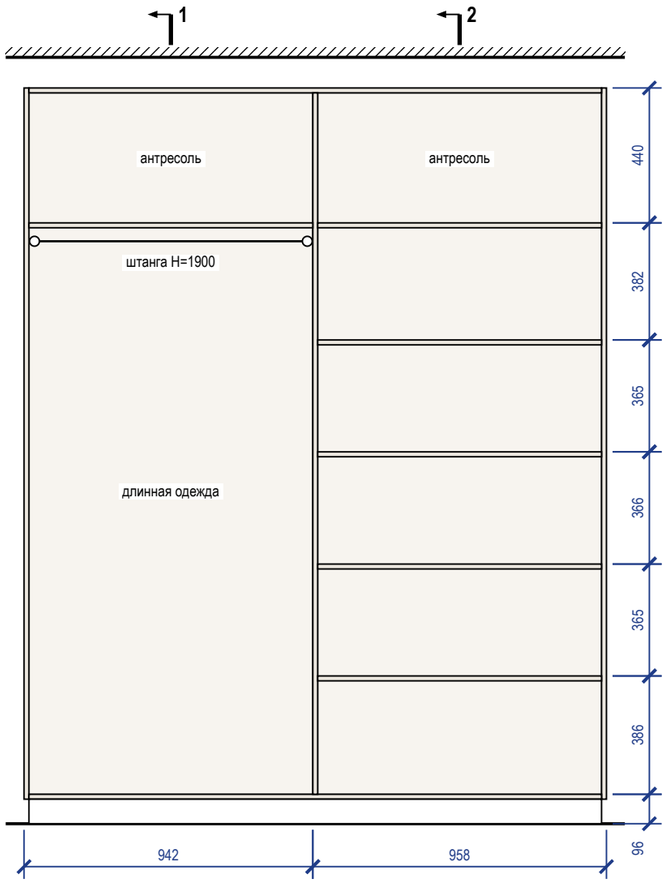

Разрез 1-1 (М 1:20)

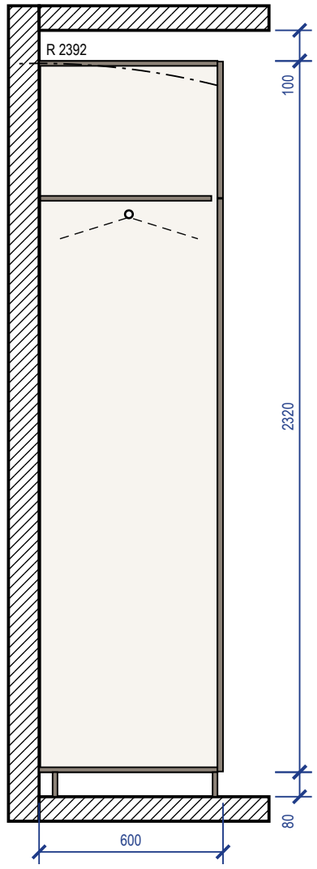


Разрез 2-2 (М 1:20)

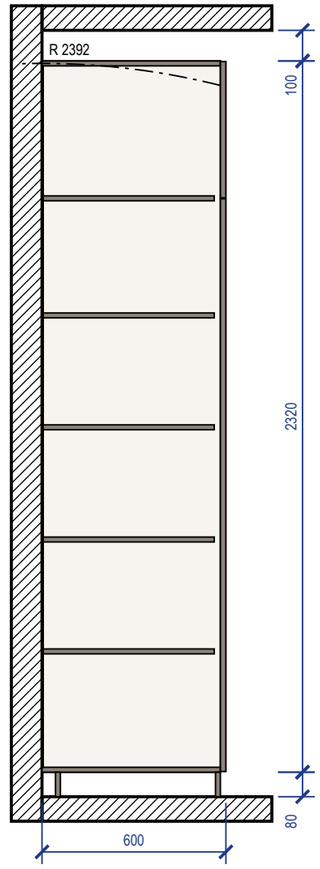

Примечания

1. Размеры — в мм по чистовой отделке; изделие 1900×600×2400 (Ш×Г×В). Перед раскроем — контрольный замер цеха после чистовой отделки стен, пола и потолка.
2. Корпус — ЛДСП 16 мм, задняя стенка ХДФ 4 мм в паз, цоколь 80 мм на регулируемых опорах; фасады накладные — МДФ 18 мм, эмаль матовая, 18 мм; цвет — по колерной карте; петли с доводчиком: фасад 1869 мм — 4 петли, фасад 445 мм — 2 петли.
3. Кромка: скрытые торцы 0,4 мм, видимые 2 мм (ПВХ/АБС).
4. Номинальные зазоры: между фасадами 3 мм, фасад — стена и фасад — потолок не менее 3 мм, фасад ящика — стойка 2 мм.
5. Присадка по 32-й системе — выполняет цех.
6. Зазор до потолка 100 мм — закрыть планкой в цвет корпуса при монтаже.
7. Подъём корпуса: диагональ боковины без цоколя $\sqrt{(2320^2 + 582^2)} = 2392$ мм < 2500 мм до потолка — корпус собирается лёжа, поднимается поворотом и ставится на цоколь.
8. Крепление к стене от опрокидывания: уголок к стене, 2 шт.; основание стены и шаг анкеров — монтажная схема шкафов.


3D орто

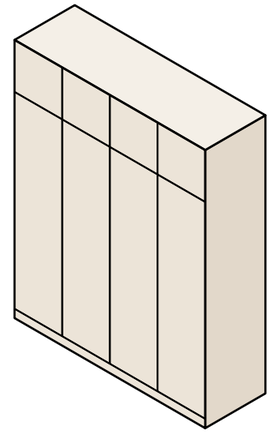


	Лист	№ док.	Подпись	Дата	Проект: Квартира 56 м²			М 1:20
Дизайнер	Кырлан А.С.			13.11.26	Шкаф распашной М-19	Стадия	Лист	Листов
Проверил						П	Д1	92
Н. контр.								
Утв.								

выпуск 13.11.2026 № 568a382a0d · стр. 70 из 92


Вид с фасадами (М 1:20)

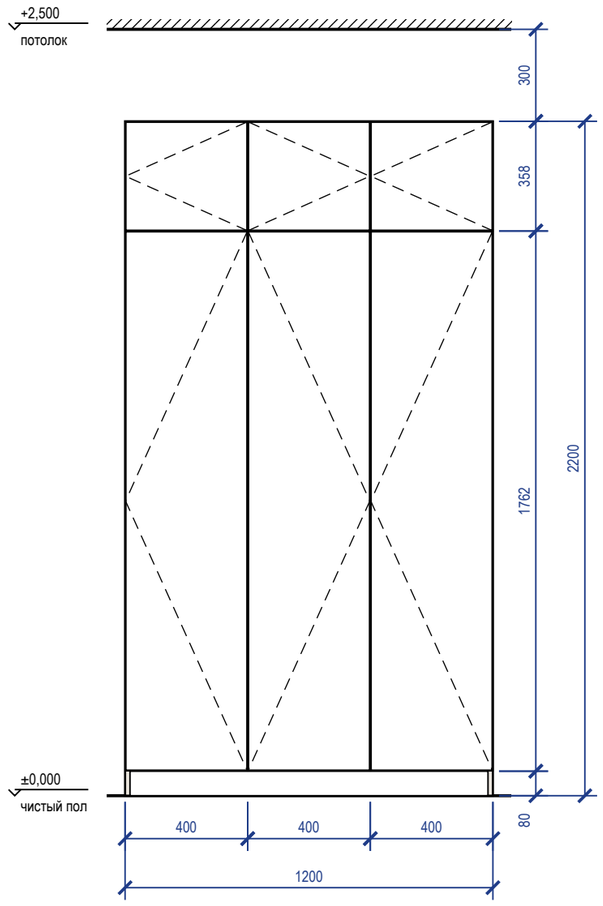


Вид без фасадов (М 1:20)

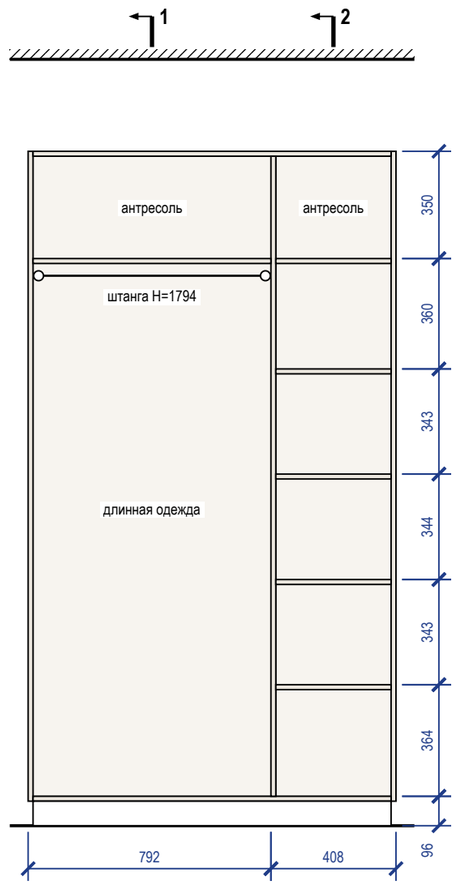

Разрез 1-1 (М 1:20)

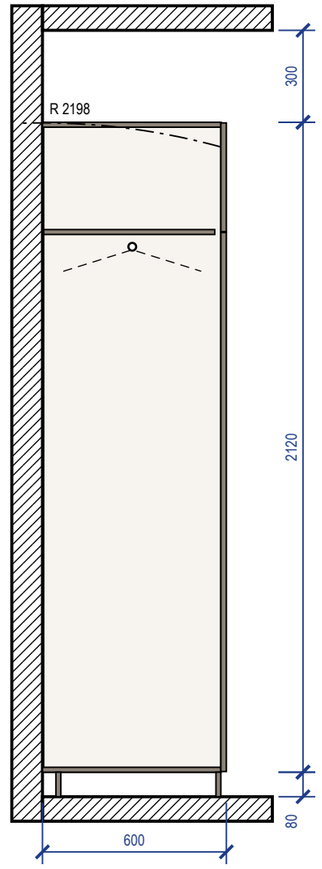


Разрез 2-2 (М 1:20)

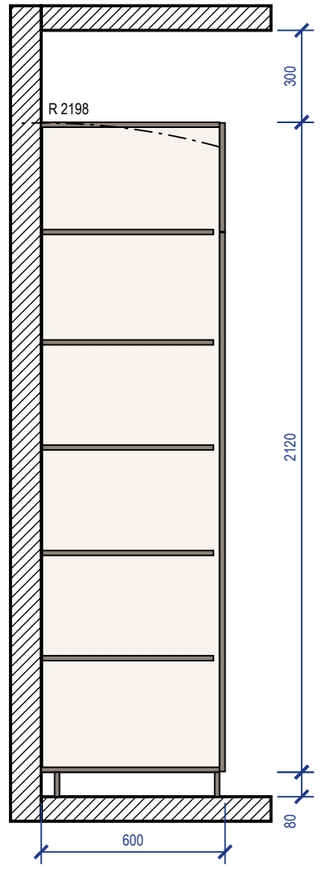

Примечания

1. Размеры — в мм по чистовой отделке; изделие 1200×600×2200 (Ш×Г×В). Перед раскроем — контрольный замер цеха после чистовой отделки стен, пола и потолка.
2. Корпус — ЛДСП 16 мм, задняя стенка ХДФ 4 мм в паз, цоколь 80 мм на регулируемых опорах; фасады накладные — МДФ 18 мм, эмаль матовая, 18 мм; цвет — по колерной карте; петли с доводчиком: фасад 1759 мм — 4 петли, фасад 355 мм — 2 петли.
3. Кромка: скрытые торцы 0,4 мм, видимые 2 мм (ПВХ/АБС).
4. Номинальные зазоры: между фасадами 3 мм, фасад — стена и фасад — потолок не менее 3 мм, фасад ящика — стойка 2 мм.
5. Присадка по 32-й системе — выполняет цех.
6. Зазор до потолка 300 мм.
7. Подъём корпуса: диагональ боковины без цоколя $\sqrt{(2120^2 + 582^2)} = 2198$ мм < 2500 мм до потолка — корпус собирается лёжа, поднимается поворотом и ставится на цоколь.
8. Крепление к стене от опрокидывания: уголок к стене, 2 шт.; основание стены и шаг анкеров — монтажная схема шкафов.


3D орто

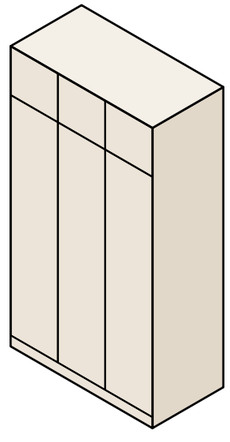


	Лист	№ док.	Подпись	Дата	Проект: Квартира 56 м²			М 1:20
Дизайнер	Кырлан А.С.			13.11.26	Шкаф распашной М-23	Стадия	Лист	Листов
Проверил						П	Д2	92
Н. контр.								
Утв.								

выпуск 13.11.2026 № 568a382a0d · стр. 71 из 92


Вид с фасадами (М 1:20)

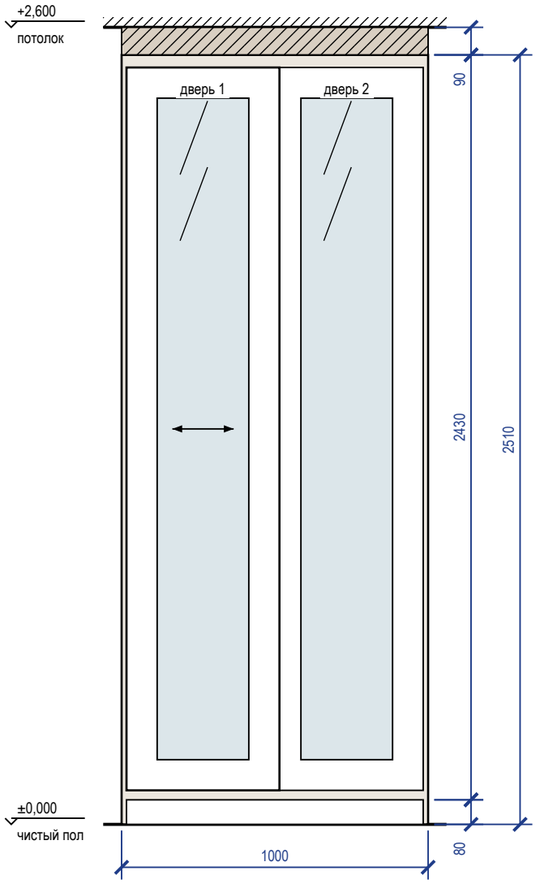


Вид без фасадов (М 1:20)

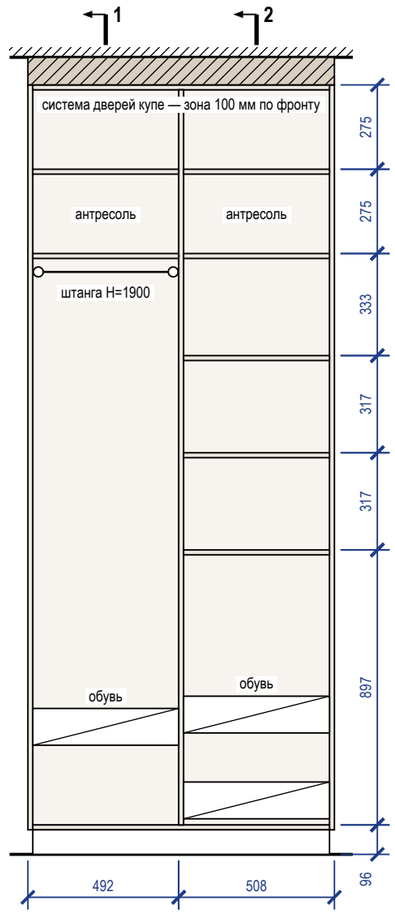

Разрез 1-1 (М 1:20)

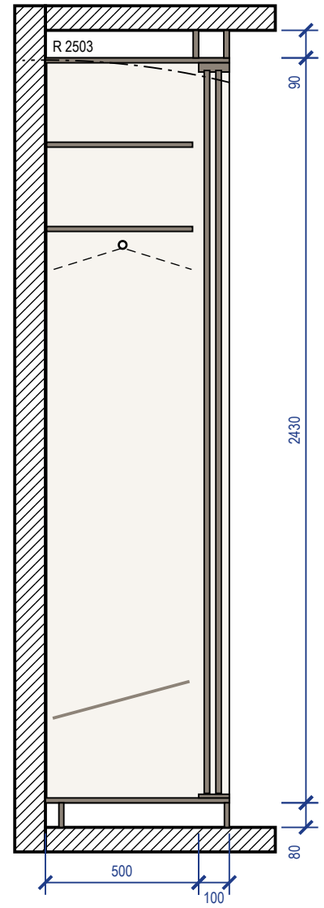


Разрез 2-2 (М 1:20)

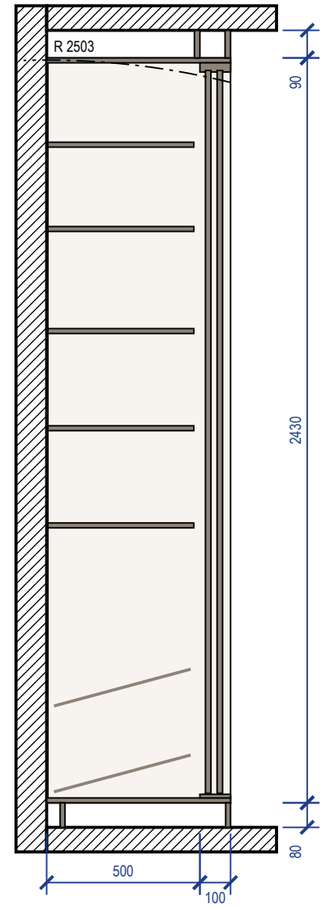

Примечания

1. Размеры — в мм по чистовой отделке; изделие 1000×600×2510 (Ш×Г×В). Перед раскроем — контрольный замер цеха после чистовой отделки стен, пола и потолка.
2. Корпус — ЛДСП 16 мм, задняя стенка ХДФ 4 мм в паз, цоколь 80 мм на регулируемых опорах; двери купе — ЛДСП 10 мм, декор «дуб натуральный» в профиле: алюминий, чёрный матовый; вставка — зеркало серебро 4 мм, плёнка безопасности; нахлёст 30 мм, ширина двери 499 мм, высота — проём минус 40 мм; цвет — по колерной карте.
3. Кромка: скрытые торцы 0,4 мм, видимые 2 мм (ПВХ/АБС).
4. Номинальные зазоры: дверь купе — боковина 3 мм, фасад ящика — стойка 2 мм; ящики внутри купе — с накладкой 30 мм на стойке со стороны нахлёста дверей.
5. Присадка по 32-й системе — выполняет цех.
6. Компенсатор 90 мм — короб из ЛДСП по фронту и торцам, подгоняется к потолку при монтаже (припуск 20 мм), крепится к корпусу и к потолку.
7. Подъём корпуса: диагональ боковины без цоколя $\sqrt{(2430^2 + 600^2)} = 2503$ мм < 2600 мм до потолка — корпус собирается лёжа, поднимается поворотом и ставится на цоколь.
8. Крепление к стене от опрокидывания — уголки 2 шт. к несущему основанию (монтажная схема шкафов).


3D орто

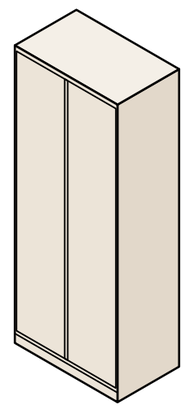


	Лист	№ док.	Подпись	Дата	Проект: Квартира 56 м²			М 1:20
Дизайнер	Кырлан А.С.			13.11.26	Шкаф-купе М-27	Стадия	Лист	Листов
Проверил						П	Д3	92
Н. контр.								
Утв.								

выпуск 13.11.2026 № 568a382a0d · стр. 72 из 92


Общий вид (М 1:20)

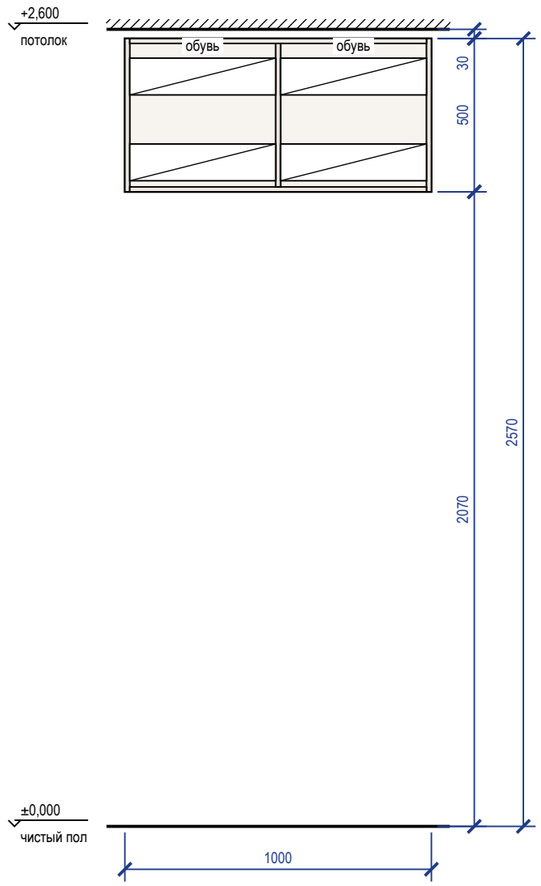

Наполнение, размеры в свету (М 1:20)

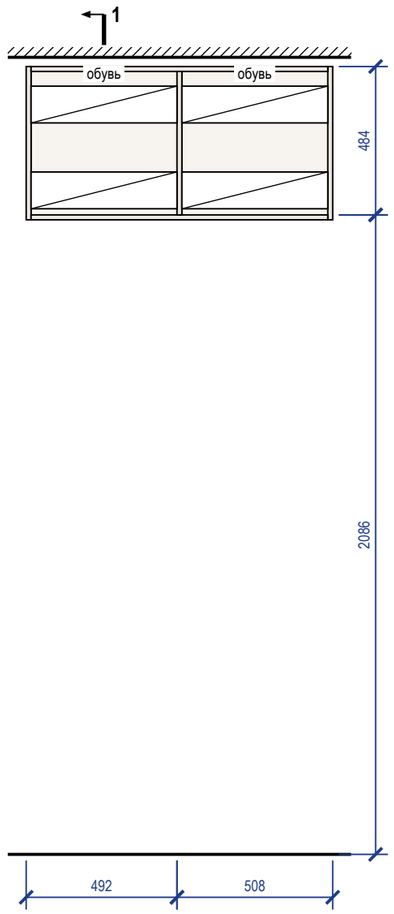


Разрез 1-1 (М 1:20)

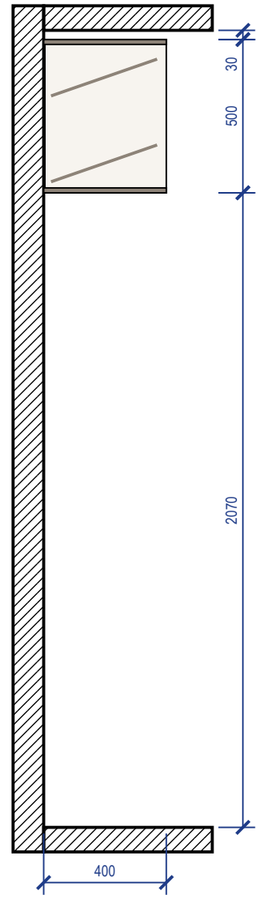

Примечания

1. Размеры — в мм по чистовой отделке; изделие 1000×400×500 (Ш×Г×В). Перед раскроем — контрольный замер цеха после чистовой отделки стен, пола и потолка.
2. Корпус — ЛДСП 16 мм, задняя стенка ХДФ 4 мм в паз, навесной корпус без цоколя, низ на 2070 мм от чистого пола; открытая система: без фасадов.
3. Кромка: скрытые торцы 0,4 мм, видимые 2 мм (ПВХ/АБС).
4. Присадка по 32-й системе — выполняет цех.
5. Зазор до потолка 30 мм — закрыть планкой в цвет корпуса при монтаже.
6. Навесной корпус — на стене: регулируемые навесы на монтажную шину или анкеры в несущее основание; основание стены и шаг анкеров — монтажная схема шкафов.

3D орто

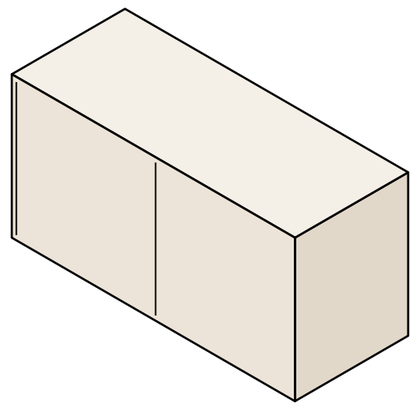

	Лист	№ док.	Подпись	Дата
Дизайнер	Кырлан А.С.			13.11.26
Проверил				
Н. контр.				
Утв.				


Проект: Квартира 56 м² — **М 1:20**

Система хранения М-29


Стадия	Лист	Листов
П	Д4	92

выпуск 13.11.2026 № 568a382a0d · стр. 73 из 92


Вид с фасадами (М 1:25)

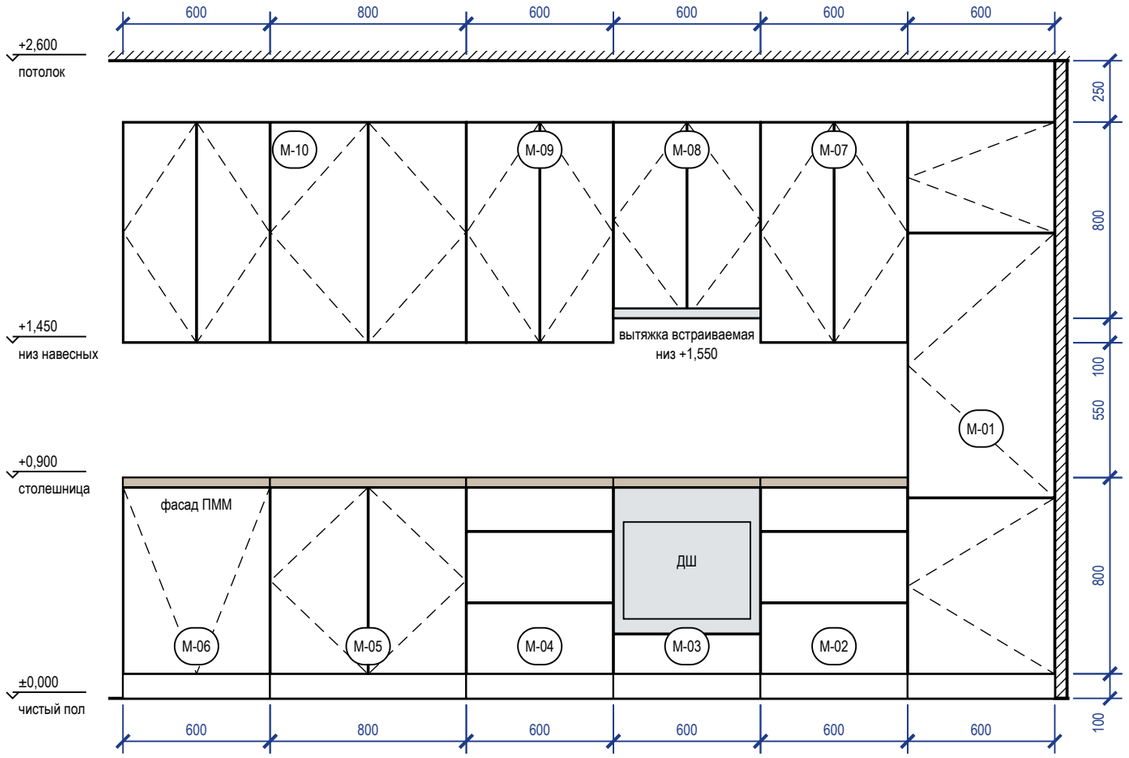


Вид без фасадов: наполнение, выводы (М 1:25)

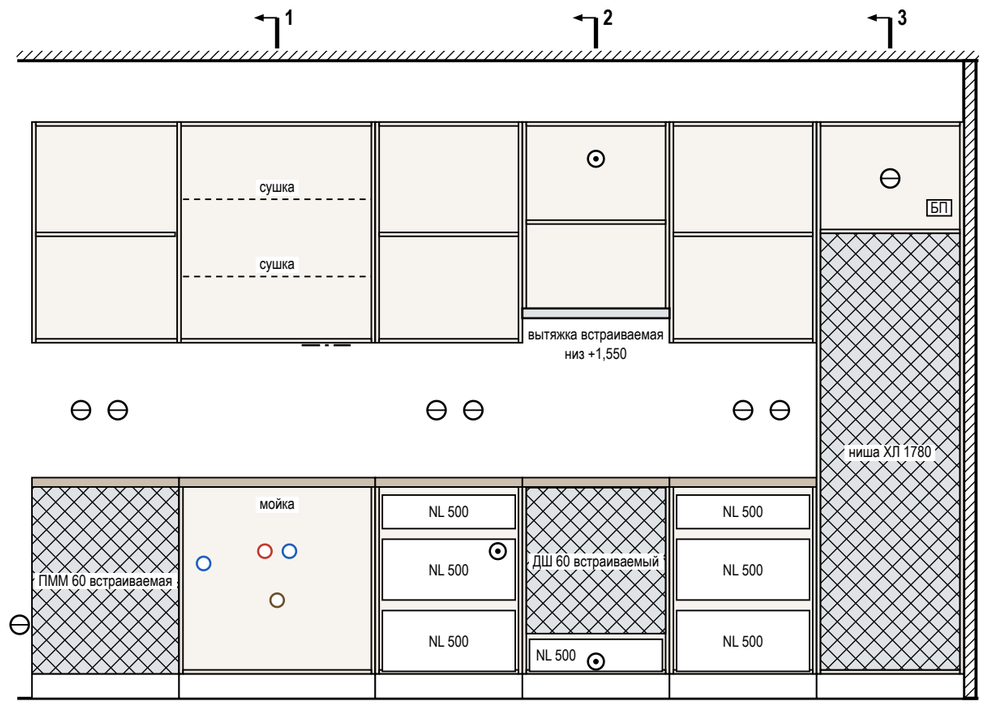


Разрез 1-1 (М 1:25)

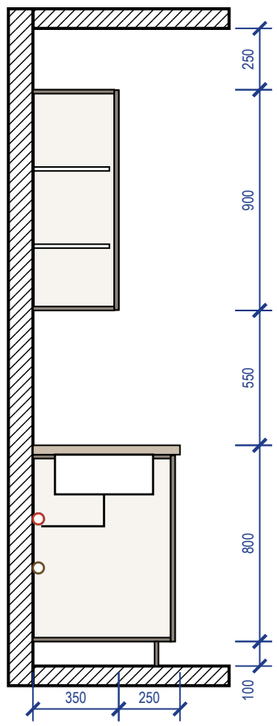


Разрез 2-2 (М 1:25)

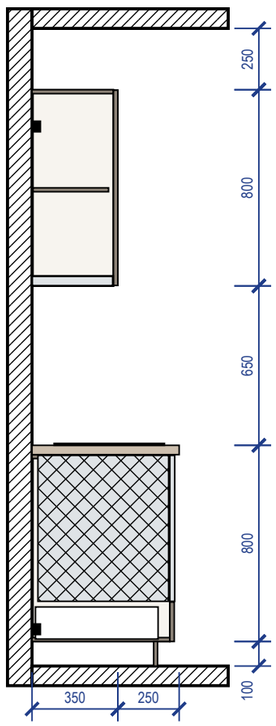

Разрез 3-3 (М 1:25)

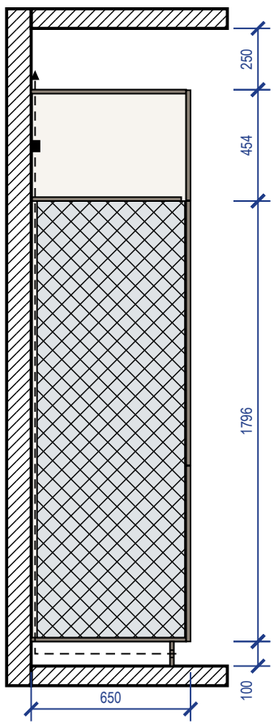

3D орто

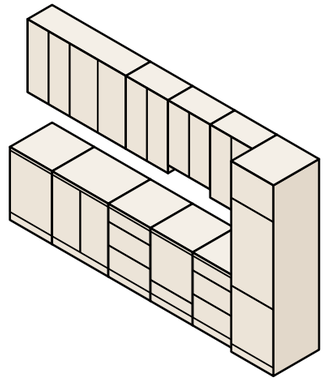

Примечания

1. Размеры — в мм по чистовой отделке, вид из помещения; марки — как на плане расстановки. Перед раскроем — контрольный замер цеха после фартука и пола.
2. Корпуса — ЛДСП 16 мм, задняя стенка ХДФ 4 мм; фасады — МДФ, эмаль матовая 18 мм, цвет по колерной карте; столешница 38 мм, свес 20 мм; цоколь 100 мм.
3. Кромка: скрытые торцы 0,4 мм, видимые 2 мм. Номинальные зазоры: между фасадами 3 мм, фасад — столешница 3 мм, фасад — стена не менее 3 мм.
4. Ящики полного выдвижения и петли — с доводчиком; присадка по 32-й системе — выполняет цех.
5. Наименования и габариты модулей (М…) — в ведомости изделий, лист 24.
6. Вытяжка встраивается в дно навесного модуля М-08 над варочной: её низ на 1550 мм от пола, 650 мм над панелью (не меньше 650 мм).
7. Ниши техники (холодильник — ориентир 1780 мм) — по монтажным схемам выбранных моделей: решётка в цоколе и канал за пеналом холодильника, зазор за духовым шкафом, фасад ПММ на двери машины.

	Лист	№ док.	Подпись	Дата	Проект: Квартира 56 м²			М 1:25
Дизайнер	Кырлан А.С.			13.11.26	Кухня (пом. 1). Развёртка гарнитура	Стадия	Лист	Листов
Проверил						П	Д5	92
Н. контр.								
Утв.								

выпуск 13.11.2026 № 568a382a0d · стр. 74 из 92

Ведомость отделки помещений (форма 1 прил. А ГОСТ 21.501-2018)

№	Наименование помещения	Потолок			Стены и перегородки			Низ стен (плинтус)			Пол		Примечание
		Вид отделки	Код цвета	S, м²	Вид отделки	Код цвета	S, м²	Вид отделки	Код цвета	L, м	Вид отделки	S, м²	
1	Гостиная-кухня 20,80 м²	ГКЛ по каркасу П113, отм. +2,600; +2,500; окраска, Tikkurila Euro Power 7, глубокоматовая, 2 слоя, подготовка Q3	Tikkurila F485	20,80	Окраска, Tikkurila Euro Power 7, колеровка по NCS, матовая, 2 слоя, подготовка Q3 Акцент — стена А: окраска, Farrow & Ball Modern Emulsion, матовая, 2 слоя, подготовка Q3 Фартук кухни (стена Г): облицовка керамогранитом, аналог: керамогранит под травертин, матовый, 1200×600×9 мм, клей C2 TE S1, затирка CG2WA	NCS S 0804-Y30R Farrow & Ball No. 298 по артикулу	30,61 10,82 1,82	Плинтус МДФ h=80 мм, аналог: МДФ под покраску 80×16	NCS S 0804-Y30R	17,5	Инженерная доска, 1167-1101, 2100×127 мм, на клею; тип 1, отм. ЧП ±0,000	20,80	Н стен 2600 (до потолка); матовая моющаяся, класс 1 EN 13300 — осознанно вместо полуматовой; плинтус в цвет: стены
2	Спальня 13,60 м²	ГКЛ по каркасу П113, отм. +2,500; +2,600; окраска, Tikkurila Euro Power 7, глубокоматовая, 2 слоя, подготовка Q3	Tikkurila F485	13,60	Окраска, Tikkurila Euro Power 7, колеровка по NCS, матовая, 2 слоя, подготовка Q3 Акцент — стена А: окраска, Tikkurila Euro Power 7, колеровка по NCS, матовая, 2 слоя, подготовка Q3	NCS S 0804-Y30R NCS S 5010-G70Y	21,86 6,33	Плинтус МДФ h=80 мм, аналог: МДФ под покраску 80×16	NCS S 0804-Y30R	13,9	Инженерная доска, 1167-1101, 2100×127 мм, на клею; тип 1, отм. ЧП ±0,000	13,60	Н стен 2500 (до потолка); за встроенной мебелью до потолка (4,75 м²) финишной отделки нет — подготовка и грунт под мебель; плинтус в цвет: стены
3	Детская 8,58 м²	ГКЛ по каркасу П113, отм. +2,500; +2,600; окраска, Tikkurila Euro Power 7, глубокоматовая, 2 слоя, подготовка Q3	Tikkurila F485	8,58	Окраска, Tikkurila Euro Power 7, колеровка по NCS, матовая, 2 слоя, подготовка Q3 Акцент — стена Г: окраска, Tikkurila Euro Power 7, матовая, 2 слоя, подготовка Q3	NCS S 0804-Y30R Tikkurila X447	19,29 6,50	Плинтус МДФ h=69 мм, SX165	NCS S 0804-Y30R	11,0	Инженерная доска, 1167-1101, 2100×127 мм, на клею; тип 1, отм. ЧП ±0,000	8,58	Н стен 2500 (до потолка); плинтус в цвет: стены
4	Санузел 4,81 м²	ГКЛВ по каркасу П113, отм. +2,600; окраска, Tikkurila Euro Power 7, матовая, 2 слоя, подготовка Q3	Tikkurila F485	4,81	Облицовка плиткой, A8UZ, 600×1200×9 мм, клей C2 TE S1, затирка CG2WA	Atlas Concorde A8UZ	19,93	нет			Аналог: керамогранит ректифицированный под травертин, матовый, 600×600×9 мм; тип 2, отм. ЧП −0,015	4,81	Н стен 2615 (до потолка); гидроизоляция обмазочная, 2 слоя, с заведением на стены 200 мм; над ванной — до 2000 и 300 мм за борт (по пирогу пола); тест проливом и акт скрытых работ
5	Прихожая 8,58 м²	ГКЛ по каркасу П113, отм. +2,600; окраска, Tikkurila Euro Power 7, глубокоматовая, 2 слоя, подготовка Q3	Tikkurila F485	8,58	Окраска, Tikkurila Euro Power 7, колеровка по NCS, матовая, 2 слоя, подготовка Q3	NCS S 0804-Y30R	17,49	Плинтус МДФ h=80 мм, аналог: МДФ под покраску 80×16	NCS S 0804-Y30R	7,5	Керамогранит, A8UZ, 600×1200×9 мм; тип 3, отм. ЧП ±0,000	8,58	Н стен 2600 (до потолка); за встроенной мебелью до потолка (4,16 м²) финишной отделки нет — подготовка и грунт под мебель; матовая моющаяся, класс 1 EN 13300 — осознанно вместо полуматовой; плинтус в цвет: стены
	Итого			**56,37**			**134,64**			**49,9**		**56,37**	

Примечания

1. Площади поверхностей — по чистым граням стен до отделки: стены = периметр × высоту от чистого пола помещения до низа потолка минус проёмы (облицовка плиткой — до верха облицовки); плинтус = периметр минус дверные проёмы; пол и потолок — по площади помещения. Количество плиток по раскладке. Площади помещений — с учётом всех частей помещения; откосы в площадь стен не входят.
2. Акцентные стены и фартук — отдельными строками, их площадь вычтена из основной отделки стен помещения; фартук — над нижними модулями кухни от столешницы до низа навесных шкафов, где шкафов нет — на 600 мм.
3. Плинтус — длина по периметру за вычетом дверных проёмов; примыкания к наличникам и встроенной мебели — по развёрткам.
4. Формат плитки — Ш×В×Т (ширина × высота в положении укладки × толщина), мм; на полу — вдоль стен А/В × вдоль стен Б/Г.
5. Коды цвета — по веерам производителей; колеровка каждой краски одной партией, проверка выкраса при свете D65 и при лампах проекта.
6. Уровни подготовки Q1–Q4 — система Knauf, не норма ГОСТ/СП; допуски поверхностей — по СП 71.13330.2017 (действующая редакция).
7. «аналог:» — изделие задано характеристиками, марку и артикул согласовать с заказчиком до закупки.
8. Сводка площадей по материалам, м²: потолок — Tikkurila F485 Euro Power 7 — 56,37; стены — NCS S 0804-Y30R Euro Power 7, колеровка по NCS 89,25; стены — Farrow & Ball No. 298 Modern Emulsion — 10,82; стены — NCS S 5010-G70Y Euro Power 7, колеровка по NCS — 6,33; стены — Tikkurila X447 Euro Power 7 — 6,50; стены — облицовка плиткой 600×1200×9 мм, Atlas Concorde A8UZ — 19,93; фартук — облицовка керамогранитом 1200×600×9 мм — 1,82.

	Лист	№ док.	Подпись	Дата	Проект: Квартира 56 м²			
Дизайнер	Кырлан А.С.			13.11.26	Ведомость отделки помещений	Стадия	Лист	Листов
Проверил						П	С1	92
Н. контр.								
Утв.								

Поз.	Наименование и техническая характеристика	Тип, марка, обозначение документа	Код продукции	Поставщик	Ед. изм.	Кол.	Образец	Примечание
	Лакокрасочные материалы							
1	Краска интерьерная водно-дисперсионная акриловая для стен, матовая, класс мокрого истирания 1 по EN 13300, база A; цвет NCS S 0804-Y30R «S 0804-Y30R», колеровка машинная	Tikkurila Euro Power 7, колеровка по NCS		Tikkurila	л	24,3		поз. К1 колерной карты; пом. 1, 2, 3, 5; S = 89,2 м² × 2 сл. × 0,12 л/м² = 21,4 л, +10 % и 0,5 л на подкраску → ≥ 24,1 л; тара 2 × 9 л + 2 × 2,7 л + 1 × 0,9 л
2	Краска интерьерная водно-дисперсионная акриловая для акцентных стен, матовая, класс мокрого истирания 1 по EN 13300, база C; цвет по вееру Farrow & Ball No. 298 «Bancha», колеровка машинная	Farrow & Ball Modern Emulsion		Farrow & Ball	л	5		поз. К2 колерной карты; пом. 1; S = 10,8 м² × 2 сл. × 0,12 л/м² = 2,6 л, +10 % и 0,5 л на подкраску → ≥ 3,4 л; тара 1 × 5 л
3	Краска интерьерная водно-дисперсионная акриловая для потолков, глубокоматовая, класс мокрого истирания 2 по EN 13300, база A; цвет по вееру Tikkurila F485 «Damask», колеровка машинная	Tikkurila Euro Power 7		Tikkurila	л	14,4		поз. К3 колерной карты; пом. 1, 2, 3, 5; S = 51,6 м² × 2 сл. × 0,12 л/м² = 12,4 л, +10 % и 0,5 л на подкраску → ≥ 14,1 л; тара 1 × 9 л + 2 × 2,7 л
4	Краска интерьерная водно-дисперсионная акриловая для акцентных стен, матовая, класс мокрого истирания 1 по EN 13300, база C; цвет NCS S 5010-G70Y «S 5010-G70Y», колеровка машинная	Tikkurila Euro Power 7, колеровка по NCS		Tikkurila	л	2,7		поз. К5 колерной карты; пом. 2; S = 6,3 м² × 2 сл. × 0,12 л/м² = 1,5 л, +10 % и 0,5 л на подкраску → ≥ 2,2 л; тара 1 × 2,7 л
5	Краска интерьерная водно-дисперсионная акриловая для акцентных стен, матовая, класс мокрого истирания 1 по EN 13300, база C; цвет по вееру Tikkurila X447 «Sea Smoke», колеровка машинная	Tikkurila Euro Power 7		Tikkurila	л	2,7		поз. К6 колерной карты; пом. 3; S = 6,5 м² × 2 сл. × 0,12 л/м² = 1,6 л, +10 % и 0,5 л на подкраску → ≥ 2,2 л; тара 1 × 2,7 л
6	Краска интерьерная водно-дисперсионная акриловая для потолков, матовая, класс мокрого истирания 1 по EN 13300, база A; цвет по вееру Tikkurila F485 «Damask», колеровка машинная	Tikkurila Euro Power 7		Tikkurila	л	1,8		поз. К8 колерной карты; пом. 4; S = 4,8 м² × 2 сл. × 0,12 л/м² = 1,2 л, +10 % и 0,5 л на подкраску → ≥ 1,8 л; тара 2 × 0,9 л
7	Краска для МДФ и дерева в цвет NCS S 0804-Y30R «S 0804-Y30R» — окраска плинтуса; блеск не ниже блеска стен	марка не задана			л	1,3		поз. К4, К7; пом. 1, 2, 3, 5; L = 49,9 м, S = 4,7 м² × 2 сл. × 0,12 л/м² + 10 %; продукт подобрать в веере NCS
8	Грунтовка акриловая под окраску стен и потолков — из системы производителя краски	по системе краски			м²	170		площадь окраски стен, акцентов и потолков; 1 слой перед окраской; расход — по ТУ грунтовки
	Плитка и керамогранит							
9	Керамогранит под травертин, 600×600×9 мм, ректификат, водопоглощение 0,1 % (BIa), противоскольжение R10, PEI IV	аналог по характеристикам			м²	6,12		шов 2 мм; Санузел, пол; по раскладке 15 шт (S = 4,81 м²), с запасом 17 шт
10	A8UZ, 600×1200×9 мм, ректификат, водопоглощение 0,1 % (BIa), противоскольжение R10, PEI IV	A8UZ		Atlas Concorde	м²	45,36		шов 2 мм; Санузел, стены А–Г; Санузел, короб инсталляции; Прихожая, пол; по раскладке 56 шт (S = 29,31 м²), с запасом 63 шт
11	Керамогранит под травертин, матовый, 1200×600×9 мм, ректификат, водопоглощение 0,1 % (BIa)	аналог по характеристикам			м²	4,32		шов 2 мм; Гостиная-кухня, фартук (ст. Г); по раскладке 5 шт (S = 1,82 м²), с запасом 6 шт
	Напольные покрытия							
12	1167-1101, рабочий слой 4 мм, эмиссия E1, укладка на клей	1167-1101		Coswick	м²	46,2		пом. 1, 2, 3; S = 43,18 м² (пол + половина стены в дверных проёмах, как в смете) + 7 %; к заказу — кратно упаковке
13	Клей для паркета и инженерной доски, эластичный (СМП / полиуретановый)	по рекомендации производителя доски			м²	44		площадь приклейки; расход и шпатель — по ТУ клея
	Погонажные изделия							
14	Плинтус МДФ под покраску 80×16, крепление к стене, окраска в цвет NCS S 0804-Y30R	аналог по характеристикам			м	43		пом. 1, 2, 5; L = 38,9 м (периметр без дверных проёмов) + 10 % на подрезку; в штуках — по длине планки
15	SX165, h = 69 мм, крепление к стене, окраска в цвет NCS S 0804-Y30R	SX165		Orac Decor	м	13		пом. 3; L = 11,0 м (периметр без дверных проёмов) + 10 % на подрезку; в штуках — по длине планки
	Смеси и материалы для облицовки							
16	Затирка для швов плитки, класс CG2WA по EN 13888	Mapei Ultracolor Plus 132		Mapei	кг	2,9		по раскладке (a+b)/(a·b) × шов × t × 1,6 + 10 %; в т. ч. 0,8 кг — позиции раскладки без марки
17	Клей плиточный C2 TE S1 по EN 12004, слой 5 мм	Ceresit CM 17		Ceresit	кг	231		10 меш. по 25 кг; 1,5 кг/м² на 1 мм слоя + 10 %; в т. ч. 68 кг — позиции раскладки без марки
18	Гидроизоляция обмазочная мокрых зон: пол, стены по периметру, зоны замачивания; 2 слоя с армирующей лентой в углах	аналог по характеристикам			м²	12,4		площадь по листу раскладки плитки + 10 %; расход смеси — по ТУ
19	Лента демпферная по периметру пола из плитки	аналог по характеристикам			м	16,9		периметр без дверных проёмов + 10 %

Примечания

1. Количества — из геометрии проекта: площади поверхностей по чистым граням стен до отделки (те же, что в ведомости отделки и колерной карте), плитка, клей и затирка — по раскладке плиточника; в графе «Кол.» — к заказу, с запасом.
2. Краска: расход 0,12 л/м² на слой в 2 слоя, если по ТУ не задан иной; запас 10 % и 0,5 л на подкраску каждого кода. Один код — одна партия, колеровка машинная в колеровочном центре бренда; в заказ — только после утверждения выкраса (колерная карта). Фасовка — по каталогу бренда на дату выпуска; к заказу — не меньше расчётного объёма.
3. «Аналог по характеристикам» — допускается изделие другого производителя с характеристиками не ниже указанных, по согласованию с автором проекта.
4. Графы «Код продукции» и «Масса 1 ед.» не заполнены: коды по классификатору продукции не присвоены, масса единицы до 25 кг (ГОСТ 21.110-2013).
5. Грунтовка и клей для доски указаны площадью обработки; объём — по ТУ выбранного продукта.

	Лист	№ док.	Подпись	Дата
Дизайнер	Кырлан А.С.			13.11.26
Проверил				
Н. контр.				
Утв.				

Проект: Квартира 56 м²

Спецификация отделочных материалов	Стадия	Лист	Листов
	П	С2	92

выпуск 13.11.2026 № 568a382a0d · стр. 76 из 92

Список покупок: материалы для магазина

№	Что купить	Артикул или характеристика	Нужно с запасом	Брать в магазине	Фасовка	Уточнить в магазине	Помещения	Кто покупает
Покрытия полов и облицовка								
1	Инженерная доска (дуб натуральный, рабочий слой 4 мм, эмиссия E1, прямая укладка)	1167-1101	46,2 м²	46,2 м²		уточнить в магазине: м² в упаковке	1, 2, 3	по проекту
2	Клей для паркетной и инженерной доски (эластичный, по ТУ изготовителя доски)	на выбор бригады по проекту	43,18 м²			уточнить в магазине: расход и фасовку — по выбранному продукту		бригада
3	Керамогранит 600×600 мм под травертин	по характеристике: керамогранит под травертин	17 шт	17 шт		уточнить в магазине: штук в коробке	4	по проекту
4	Керамогранит 600×1200 мм A8UZ	A8UZ	62 шт	63 шт		уточнить в магазине: штук в коробке	4, 5	по проекту
5	Керамогранит 1200×600 мм под травертин, матовый	по характеристике: керамогранит под травертин, матовый	6 шт	6 шт		уточнить в магазине: штук в коробке	1	по проекту
Сухие смеси и гидроизоляция								
6	Клей плиточный цементный класса C2 TE S1 (ГОСТ Р 56387-2018)	Ceresit CM 17 или аналог	230,25 кг	10 меш.	мешок 25 кг			по проекту
7	Затирка цементная класса CG2WA, цвет — по колерной карте	Mapei Ultracolor Plus 132 или аналог	2,88 кг	2 упак.	упак. 2 кг			по проекту
8	Гидроизоляция обмазочная полимерная, 2 слоя, лента в углах, манжеты на выводах	на выбор бригады по проекту	12,42 м²			уточнить в магазине: расход и фасовку — по выбранному продукту	4	бригада
9	Лента демпферная по периметру пола из плитки	на выбор бригады по проекту	16,93 м	17 м		уточнить в магазине: фасовку		бригада
10	Смесь цементно-песчаная для стяжки М200 (50 мм, 33 мм)	на выбор бригады по проекту	2,91 м³			уточнить в магазине: расход и фасовку — по выбранному продукту		бригада
11	Смесь штукатурная гипсовая для машинного и ручного нанесения по маякам, слой до 10 мм	на выбор бригады по проекту	148,23 м²			уточнить в магазине: расход и фасовку — по выбранному продукту	1, 2, 3, 4, 5	бригада
Короба из ГКЛВ								
12	Лист ГКЛВ 12,5 мм, 2500 × 1200 мм, обшивка коробов в 2 слоя	на выбор бригады по проекту	3,87 м²	2 лист.	лист 3,00 м²		4	бригада
13	Профиль стальной оцинкованный 27 × 28 мм: каркас коробов (стойки и направляющие)	на выбор бригады по проекту	9,46 м	4 шт	хлыст 3 м			бригада
Перегородки и облицовки из ГКЛВ								
14	Лист ГКЛ 12,5 мм, 2500 × 1200 мм: обшивка перегородок и облицовок, 2 слоя на сторону	на выбор бригады по проекту	23,5 м²	8 лист.	лист 3,00 м²			бригада
15	Профиль направляющий ПН 100: по потолку и полу, перемычки над проёмами	на выбор бригады по проекту	5,72 м	2 шт	хлыст 3 м			бригада
16	Профиль стоечный ПС 100: стойки через шаг каркаса и короткие над проёмами	на выбор бригады по проекту	12,54 м	5 шт	хлыст 3 м			бригада
17	Профиль усиленный УА 100 (2,0 мм): стойки по краям проёма на полную высоту	на выбор бригады по проекту	5,94 м	2 шт	хлыст 3 м			бригада
18	Плита минераловатная звукопоглощающая в полость каркаса, толщина по глубине профиля 100 мм	на выбор бригады по проекту	5,87 м²			уточнить в магазине: расход и фасовку — по выбранному продукту		бригада
19	Лента уплотнительная самоклеящаяся под профили по потолку, полу и у примыканий к стенам	на выбор бригады по проекту	10,78 м	11 м		уточнить в магазине: фасовку		бригада
20	Саморезы для ГКЛ по металлу (по слоям обшивки), дюбели для направляющих — по ТУ изготовителя системы	на выбор бригады по проекту	21,36 м²			уточнить в магазине: расход и фасовку — по выбранному продукту		бригада
Перегородки из кладки								
21	Пеноблок D500: изделия кладки толщиной 100 мм	на выбор бригады по проекту	0,56 м³			уточнить в магазине: расход и фасовку — по выбранному продукту		бригада
22	Смесь кладочная для блоков (клей или раствор — по виду изделия)	на выбор бригады по проекту	0,56 м³ кладки			уточнить в магазине: расход и фасовку — по выбранному продукту		бригада
23	Перемычка над проёмом в кладке П-1: L 1200 мм	на выбор бригады по проекту	1 шт	1 шт	шт			бригада
24	Кирпич керамический полнотелый: изделия кладки толщиной 120 мм	на выбор бригады по проекту	1,3 м³			уточнить в магазине: расход и фасовку — по выбранному продукту		бригада

	Лист	№ док.	Подпись	Дата	Проект: Квартира 56 м²			
Дизайнер	Кырлан А.С.			13.11.26				
Проверил					Список покупок	Стадия	Лист	Листов
Н. контр.								
Утв.						П	С3	92

выпуск 13.11.2026 № 568a382a0d · стр. 77 из 92

Список покупок: материалы для магазина (продолжение)

№	Что купить	Артикул или характеристика	Нужно с запасом	Брать в магазине	Фасовка	Уточнить в магазине	Помещения	Кто покупает
25	Смесь кладочная для кирпича (клей или раствор — по виду изделия)	на выбор бригады по проекту	1,3 м³ кладки			уточнить в магазине: расход и фасовку — по выбранному продукту		бригада
Слаботочные сети								
26	Кабель домофона — тип по системе поставщика	на выбор бригады по проекту	6,7 м	7 м		уточнить в магазине: длину бухты		бригада
27	Кабель коаксиальный RG-6 (75 Ом) к розеткам ТВ	на выбор бригады по проекту	11,7 м	12 м		уточнить в магазине: длину бухты		бригада
28	Кабель U/UTP кат. 6 (LAN, Wi-Fi и камеры по PoE)	на выбор бригады по проекту	44,9 м	45 м		уточнить в магазине: длину бухты		бригада
29	Гофротруба Ø20 для слаботочных линий, отдельно от силовых	на выбор бригады по проекту	57 м	57 м		уточнить в магазине: длину бухты		бригада
30	Розетка компьютерная RJ45, кат. 6, с рамкой и подрозетником	на выбор бригады по проекту	3 шт	3 шт	шт			бригада
31	Розетка телевизионная (коаксиальная) с рамкой и подрозетником	на выбор бригады по проекту	1 шт	1 шт	шт			бригада
32	Трубка или монитор домофона (поставка домофонной организации)	на выбор бригады по проекту	1 шт	1 шт	шт			по проекту
33	Щит слаботочный ЩС: корпус, DIN-рейка, розетки 220 В	на выбор бригады по проекту	1 шт	1 шт	шт			бригада
34	Патч-панель, портов не менее 5	на выбор бригады по проекту	1 шт	1 шт	шт			бригада
Лакокрасочные материалы								
35	Краска интерьерная акриловая, матовая, класс истирания 1	Farrow & Ball Modern Emulsion No. 298 «Bancha»	2,86 л	2 банк.	банка 2,5 л		1	по проекту
36	Краска интерьерная акриловая, матовая, класс истирания 1	Tikkurila Euro Power 7, колеровка по NCS S 0804-Y30R «S 0804-Y30R»	23,56 л	9 банк.	банка 2,7 л		1, 2, 3, 5	по проекту
37	Краска интерьерная акриловая, глубокоматовая, класс истирания 2	Tikkurila Euro Power 7 F485 «Damask»	13,61 л	6 банк.	банка 2,7 л		1, 2, 3, 5	по проекту
38	Краска интерьерная акриловая, матовая, класс истирания 1	Tikkurila Euro Power 7, колеровка по NCS S 5010-G70Y «S 5010-G70Y»	1,67 л	1 банк.	банка 2,7 л		2	по проекту
39	Краска интерьерная акриловая, матовая, класс истирания 1	Tikkurila Euro Power 7 X447 «Sea Smoke»	1,72 л	1 банк.	банка 2,7 л		3	по проекту
40	Краска интерьерная акриловая, матовая, класс истирания 1	Tikkurila Euro Power 7 F485 «Damask»	1,26 л	1 банк.	банка 2,7 л		4	по проекту
41	Шпаклёвка финишная полимерная под окраску (стены и потолки, Q3)	на выбор бригады по проекту	196 м²			уточнить в магазине: расход и фасовку — по выбранному продукту		бригада
42	Грунтовка акриловая глубокого проникновения, 2 слоя	на выбор бригады по проекту	221,98 м²			уточнить в магазине: расход и фасовку — по выбранному продукту		бригада
Погонажные изделия и потолки								
43	Плинтус напольный МДФ под покраску, h=80 мм, крепление к стене	по характеристике: плинтус МДФ под покраску 80×16	42,79 м.п.	18 шт	хлыст 2,4 м		1, 2, 5	по проекту
44	Плинтус напольный МДФ под покраску, h=69 мм, крепление к стене	SX165	12,1 м.п.	6 шт	хлыст 2,4 м		3	по проекту
45	Потолок подвесной ГКЛ/ГКЛВ по каркасу Knauf П113: листы, профили, подвесы, лента, шпаклёвка швов	Knauf П113	56,37 м²		комплект	уточнить в магазине: расход и фасовку — по выбранному продукту		по проекту

Примечания

1. «Нужно с запасом» — расход по чертежам и раскладке плюс запас на подрезку и подкраску; «Брать в магазине» — то же количество в единицах, которыми продают (банки, мешки, упаковки, листы, штуки, литры).
2. «Уточнить в магазине» — фасовки этого товара в проекте нет: спросите у продавца, сколько в упаковке, и возьмите целое число упаковок не меньше «Нужно с запасом».
3. Плитку, доску и краску одного цвета берите одной партией (один калибр и тон на помещение) и сохраните чек и номер партии до конца ремонта.
4. «По характеристике» — артикул не выбран: подойдёт любой товар с этими свойствами, согласуйте его с дизайнером до покупки. «Бригада» материал выбирает и закупает бригада по своей технологии.
5. Помещения: 1 — Гостиная-кухня; 2 — Спальня; 3 — Детская; 4 — Санузел; 5 — Прихожая; «—» — материал для нескольких помещений, расход по месту.

	Лист	№ док.	Подпись	Дата	Проект: Квартира 56 м²			
Дизайнер	Кырлан А.С.			13.11.26	Список покупок (окончание)	Стадия	Лист	Листов
Проверил						П	С4	92
Н. контр.								
Утв.								

выпуск 13.11.2026 № 568a382a0d · стр. 78 из 92

Смета проекта: весь проект по категориям (прайсы собраны 21.09.2026, часть расценок сверена повторно 06.10.2026 и 08.11.2026)

Категория	Позиций	С ценой	По КП	Сумма по позициям с ценой, ₽
Ремонт: работы	56	35	21	786 791
Ремонт: материалы отделки и черновые	41	14	27	497 009
Электрика: кабель, механизмы, щит	40	0	40	
Сантехника: приборы, трубы, арматура	32	0	32	
Доставка и услуги	4	1	3	49 701
Мебель (включая кухню)	26	0	26	
Свет: светильники и ленты	46	0	46	
Техника	6	0	6	
Декор и текстиль	53	0	53	
ИТОГО по позициям с ценой (цены — нижняя граница открытых прайсов)	**304**	**50**	**254**	**1 333 501**
Резерв на непредвиденные работы и материалы, 15 % от ремонта				200 025
ВЕСЬ ПРОЕКТ — вилка «от … до …», ₽				**1 333 501 … 1 533 526**
Позиции «по КП» — цена не названа, в итог НЕ входят: работы — 21; материалы отделки и черновые — 27; электрика: кабель, механизмы, щит — 40; сантехника: приборы, трубы, арматура — 32; доставка и услуги — 3; мебель (включая кухню) — 26; свет: светильники и ленты — 46; техника — 6; декор и текстиль — 53			**254**	**итог выше на их цену**

По этапам

Этап	Поз.	С ценой	Сумма, ₽
Демонтаж и черновые работы (работы)	15	6	206 611
Инженерные системы (работы)	22	12	153 000
Чистовые работы (работы)	19	17	427 180
Черновые материалы (смеси, ГКЛ, гидроизоляция)	24	2	20 000
Электрика: кабель, механизмы, щит, слаботочка	40	0	
Сантехника: приборы, трубы, арматура	32	0	
Чистовые материалы (отделка, двери)	17	12	477 009
Доставка и услуги	4	1	49 701
Резерв на непредвиденное, 15 %	1	1	200 025
Итого ремонт (с резервом)			**1 533 526**

По помещениям

Помещение	Работы, ₽	Материалы, ₽	Всего, ₽
Общее по объекту (без привязки к помещению)	48 200		48 200
1. Гостиная-кухня	237 473	151 035	388 508
2. Спальня	157 162	85 851	243 013
3. Детская	113 118	57 537	170 655
4. Санузел	131 686	147 575	279 261
5. Прихожая	99 152	55 011	154 163
Доставка и услуги			49 701
Резерв 15 %			200 025
Итого ремонт (с резервом)			**1 533 526**

Работы по этапам с расценками (ориентир)

№	Работа	Ед.	Объём	Расценка, ₽	Сумма, ₽	Расценка	Чей подряд
1. Демонтаж и черновые работы — работы, ориентир по открытым прайсам							
1	Демонтаж существующего покрытия пола до основания	м²	56,37	по КП			бригада
2	Демонтаж существующей отделки стен до основания	м²	145,43	по КП			бригада
3	Демонтаж существующей отделки потолка до основания	м²	56,37	по КП			бригада
4	Демонтаж существующих дверных блоков	шт	5,00	по КП			бригада

	Лист	№ док.	Подпись	Дата	Проект: Квартира 56 м²			
Дизайнер	Кырлан А.С.			13.11.26				
Проверил					Смета проекта: этапы, помещения, итог	Стадия	Лист	Листов
Н. контр.						П	С5	92
Утв.								

Работы по этапам с расценками (ориентир) (продолжение)

№	Работа	Ед.	Объём	Расценка, ₽	Сумма, ₽	Расценка	Чей подряд
5	Демонтаж существующих сантехприборов и электрооборудования (если есть)	компл		по КП			бригада
6	Кладка перегородки П-1 (блоки, толщина 100 мм): Пеноблок D500, армирование через 2 ряда, штукатурка с двух сторон.	м²	5,55	по КП			бригада
7	Кладка перегородки П-3 (кирпич, толщина 120 мм): Кирпич керамический полнотелый, кладка в полкирпича, штукатурка с двух сторон.	м²	10,80	по КП			бригада
8	Устройство перемычек над проёмами в кладке П-1.	шт	1,00	по КП			бригада
9	Монтаж каркасной перегородки П-2 (С112): каркас ПС усиленный через 600 мм, ГКЛ в 2 слоя с каждой стороны, обрамление проёма профилем УА.	м²	5,34	2 700	14 418	Ц1	бригада
10	Заполнение каркаса П-2 минераловатной плитой (звукоизоляция, Rw 51 дБ).	м²	5,34	по КП			бригада
11	Устройство стяжки: стяжка ЦПС М200, 50 мм	м²	56,97	530	30 194	Ц1	бригада
12	Гидроизоляция обмазочная, 2 слоя: пол, стены на 200 мм, зоны замачивания	м²	11,29	450	5 081	Ц1	бригада
13	Штукатурка стен по маякам, до 10 мм	м²	134,75	530	71 418	Ц1	бригада
14	Штукатурка оконных откосов шириной до 200 мм	м²	1,75	540	945	Ц4	бригада
15	Потолок ГКЛ по каркасу П113, 1 слой	м²	56,37	1 500	84 555	Ц1	бригада
2. Инженерные системы — работы, ориентир по открытым прайсам							
16	Прокладка кабеля ВВГнг(А)-LS по группам щита: за потолком и в штробах стен (штробы — только после технического заключения, см. строку «Штробы в стенах»)	м	366,20	60	21 972	Ц3	бригада
17	Прокладка слаботочной линии: Кабель домофона — тип по системе поставщика, отдельно от силовых	м	6,70	по КП			бригада
18	Прокладка слаботочной линии: Кабель коаксиальный RG-6 (75 Ом) к розеткам ТВ, отдельно от силовых	м	11,70	по КП			бригада
19	Прокладка слаботочной линии: Кабель U/UTP кат. 6 (LAN, Wi-Fi и камеры по PoE), отдельно от силовых	м	44,90	по КП			бригада
20	Прокладка гофротрубы Ø20 для слаботочных линий, отдельно от силовых	м	57,00	140	7 980	Ц3	бригада
21	Сборка слаботочного щита ЩС: корпус, патч-панель, подключение линий и питания 220 В; коммутатор и точки доступа — оборудование заказчика	шт	1,00	по КП			бригада
22	Электроточка: подрозетник в бетоне, розетка, выключатель, вывод	шт	55,00	950	52 250	Ц3	бригада
23	Штробы в стенах под спуски кабеля к точкам — выполняются только после технического заключения о несущих стенах	м	91,05	по КП			бригада
24	Установка встраиваемого точечного светильника	шт	33,00	750	24 750	Ц3	бригада
25	Монтаж светильника: потолочного, подвесного, настенного	шт	8,00	1 200	9 600	Ц3	бригада
26	Монтаж LED-ленты в алюминиевый профиль	м	31,60	230	7 268	Ц3	бригада
27	Установка блока питания LED в доступном месте (люк, шкаф)	шт	5,00	570	2 850	Ц3	бригада
28	Установка автономного пожарного извещателя	шт	5,00	по КП			бригада
29	Сборка щита: установка автоматов и АВДТ групп, вводного автомата	шт	15,00	230	3 450	Ц3	бригада
30	Установка вводного УЗО	шт	1,00	380	380	Ц3	бригада
31	Монтаж инсталляции, установка подвесного унитаза и кнопки смыва	шт	1,00	10 500	10 500	Ц1	бригада
32	Короб инсталляции: каркас и обшивка ГКЛВ в 2 слоя, ревизионный доступ к смыву	шт	1,00	по КП			бригада
33	Короб К1 над чистым полом: каркас и обшивка ГКЛВ под плитку (материалы — в спецификации ВК)	м	8,77	по КП			бригада
34	Установка ванны с сифоном	шт	1,00	6 000	6 000	Ц1	бригада
35	Установка умывальника (мойки) с сифоном и смесителем	шт	2,00	3 000	6 000	Ц1	бригада
36	Подключение стиральной (посудомоечной) машины к ВК	шт	2,00	по КП			бригада

	Лист	№ док.	Подпись	Дата	Проект: Квартира 56 м²			
Дизайнер	Кырлан А.С.			13.11.26	Смета проекта: этапы, помещения, итог (продолжение)	Стадия	Лист	Листов
Проверил						П	С6	92
Н. контр.								
Утв.								

выпуск 13.11.2026 № 568a382a0d · стр. 80 из 92

Работы по этапам с расценками (ориентир) (продолжение)

№	Работа	Ед.	Объём	Расценка, ₽	Сумма, ₽	Расценка	Чей подряд
37	Установка радиатора с узлом подключения и терморегулятором	шт	3,00	по КП			бригада
3. Чистовые работы — работы, ориентир по открытым прайсам							
38	Облицовка стен керамогранитом 600×1200 на клею	м²	18,97	2 500	47 425	Ц5	бригада
39	Облицовка короба инсталляции (ГКЛВ) керамогранитом: лицо, боковины, полка	м²	1,76	2 500	4 400	Ц5	бригада
40	Облицовка фартука керамогранитом 1200×600	м²	1,82	2 400	4 368	Ц2	бригада
41	Укладка керамогранита на пол, 600×600, на клею	м²	13,79	1 800	24 822	Ц2	бригада
42	Затирка швов керамогранита	м²	35,94	150	5 391	Ц2	бригада
43	Грунтование стен, 2 слоя (под штукатурку и под отделку)	м²	145,43	96	13 961	Ц4	бригада
44	Шпаклёвка стен под окраску, 2 слоя (старт и финиш), уровень Q3	м²	121,81	750	91 358	Ц1	бригада
45	Грунтование и шпаклёвка оконных откосов, 2 слоя	м	13,50	300	4 050	Ц4	бригада
46	Грунтование потолка, 2 слоя	м²	56,37	96	5 412	Ц4	бригада
47	Шпаклёвка потолка под окраску, 2 слоя, уровень Q3	м²	56,37	950	53 552	Ц1	бригада
48	Окраска потолка водно-дисперсионной краской, 2 слоя	м²	56,37	360	20 293	Ц1	бригада
49	Окраска стен водно-дисперсионной краской, 2 слоя	м²	134,29	300	40 287	Ц1	бригада
50	Окраска оконных откосов, 2 слоя	м	13,50	120	1 620	Ц4	бригада
51	Укладка инженерной доски на клей	м²	43,18	1 200	51 816	Ц1	бригада
52	Установка плинтуса МДФ h=80 мм	м	49,90	450	22 455	Ц1	бригада
53	Окраска плинтуса в тоне S 0804-Y30R, 2 слоя	м	49,90	300	14 970	Ц1	бригада
54	Монтаж дверей скрытого монтажа под покраску (поставщик дверей)	шт	4,00	5 250	21 000	Ц1	поставщик
55	Входная дверь, поставка с монтажом и откосами	шт	1,00	по КП			поставщик
56	Монтаж телевизора ОБ-01 на кронштейн, скрытая прокладка HDMI и питания (штроба, трубка), подключение акустики	шт	1,00	по КП			бригада
4. Прочие работы и услуги — работы, ориентир по открытым прайсам							
57	Кухонный гарнитур по проекту кухни, изготовление и монтаж (4–8 нед.)	компл	1,00	по КП			поставщик
	Итого работы (позиции с расценкой)				**786 791**		

Примечания

1. Итог «ВЕСЬ ПРОЕКТ» — не прогноз, а сумма того, у чего есть цена: ремонт (работы и материалы по смете сметчика), мебель, свет, техника и декор — по ценам из данных проекта. Позиции без цены названы «по КП» (254 шт.) и в итог не входят: пока цена не названа, итог выше напечатанного.
2. Вилка: «от» — сумма по позициям с ценой по нижней границе открытых прайсов (прайсы собраны 21.09.2026, часть расценок сверена повторно 06.10.2026 и 08.11.2026, Москва); «до» — «от» плюс резерв на непредвиденное (15 % от ремонта; частный ремонт 10–20 %).
3. Работы — ориентир по прайсам подрядчиков, не договорная цена: расценку называет бригада после контрольного обмера. Материалы — по «Смете материалов с ценами» (следующий лист).
4. Разбивка по помещениям — доли: общая закупка делится пропорционально площади (длине, числу), по которой считается позиция; работы — по объёму строки в помещении. Сумма по помещениям, по этапам и по категориям одна и та же.
5. Источники расценок и цен: Ц1 — Домашний мастерок: прайс на отделочные работы, 2026; Ц2 — Домашний мастерок: прайс на плиточные работы, 2026; Ц3 — Домашний мастерок: прайс на электромонтажные работы, 2026; Ц4 — Профи ремонтник: штукатурно-малярные работы; Ц5 — Profi.ru: укладка керамогранита на стены, Москва 2026; Ц6 — справочник материалов: ориентир по сегментам; Ц7 — Розница Москвы, 09.2026: Лемана ПРО, KGSnab, официальный дилер Farrow & Ball.
6. Оборудование «по КП» из сметы сметчика (кухня и др.): 1 поз. — в позиции «по КП» мебели и техники.

	Лист	№ док.	Подпись	Дата	Проект: Квартира 56 м²			
Дизайнер	Кырлан А.С.			13.11.26				
Проверил					Смета проекта: этапы, помещения, итог (окончание)	Стадия	Лист	Листов
Н. контр.								
Утв.						П	С7	92

выпуск 13.11.2026 № 568a382a0d · стр. 81 из 92

Смета материалов с ценами

№	Позиция	Ед.	Нетто	Запас	С запасом	К закупке (упаковка)	Цена за ед., ₽	Сумма, ₽	Заказать заранее	Доп.
Чистовая отделка — позиций 17, с ценой 12, итого 477 009 ₽										
Покрытия полов и облицовка										
1	Инженерная доска (дуб натуральный, рабочий слой 4 мм, эмиссия E1, прямая укладка) — 1167-1101	м²	43,18	7 %	46,20	46,20 м²	4 513 / м²	208 501		8
2	Керамогранит 600×600 мм под травертин — керамогранит под травертин	шт	15	13 %	17	17 шт · коробка	1 800 / м²	11 016		1, 8
3	Керамогранит 600×1200 мм A8UZ	шт	56	13 %	63	63 шт · коробка	3 500 / м²	158 760		8
4	Керамогранит 1200×600 мм под травертин, матовый — керамогранит под травертин, матовый	шт	5	20 %	6	6 шт · коробка	3 500 / м²	15 120		1, 8
Лакокрасочные материалы										
5	Краска интерьерная акриловая, матовая, класс истирания 1 — Farrow & Ball Modern Emulsion No. 298 «Bancha»	л	2,60	10 %	2,86	2 банка · банка 2,5 л	5 800 / банк	11 600		8
6	Краска интерьерная акриловая, матовая, класс истирания 1 — Tikkurila Euro Power 7, колеровка по NCS S 0804-Y30R «S 0804-Y30R»	л	21,42	10 %	23,56	9 банка · банка 2,7 л	3 510 / банк	31 590		8
7	Краска интерьерная акриловая, глубокоматовая, класс истирания 2 — Tikkurila Euro Power 7 F485 «Damask»	л	12,37	10 %	13,61	6 банка · банка 2,7 л	3 510 / банк	21 060		8
8	Краска интерьерная акриловая, матовая, класс истирания 1 — Tikkurila Euro Power 7, колеровка по NCS S 5010-G70Y «S 5010-G70Y»	л	1,52	10 %	1,67	1 банка · банка 2,7 л	3 510 / банк	3 510		8
9	Краска интерьерная акриловая, матовая, класс истирания 1 — Tikkurila Euro Power 7 X447 «Sea Smoke»	л	1,56	10 %	1,72	1 банка · банка 2,7 л	3 510 / банк	3 510		8
10	Краска интерьерная акриловая, матовая, класс истирания 1 — Tikkurila Euro Power 7 F485 «Damask»	л	1,15	10 %	1,26	1 банка · банка 2,7 л	3 510 / банк	3 510		8
Погонажные изделия и потолки										
11	Плинтус напольный МДФ под покраску, h=80 мм, крепление к стене — плинтус МДФ под покраску 80×16	м	38,90	10 %	42,79	18 шт · хлыст 2,4 м	368 / шт	6 624		1, 8
12	Плинтус напольный МДФ под покраску, h=69 мм, крепление к стене — SX165	м	11,00	10 %	12,10	6 шт · хлыст 2,4 м	368 / шт	2 208		8
Двери										
13	Дверь входная Д-1, проём 1000×2100 мм	шт	1		1	1 шт	по запросу			6
14	Дверь скрытого монтажа (короб под покраску) Д-2, проём 900×2100 мм, UNION FILO-60 / INVISIBLE ФИЛО-60, ГРУНТ; ИНВИЗИБЛ | FILO-60, FONDO; INVISIBLE	шт	1		1	1 шт	по запросу		≈ 30 дн.	6, 7
15	Дверь скрытого монтажа (короб под покраску) Д-3, проём 900×2100 мм, UNION FILO-60 / INVISIBLE ФИЛО-60, ГРУНТ; ИНВИЗИБЛ | FILO-60, FONDO; INVISIBLE	шт	1		1	1 шт	по запросу		≈ 30 дн.	6, 7
16	Дверь скрытого монтажа (короб под покраску) Д-4, проём 800×2100 мм, UNION FILO-60 / INVISIBLE ФИЛО-60, ГРУНТ; ИНВИЗИБЛ | FILO-60, FONDO; INVISIBLE	шт	1		1	1 шт	по запросу		≈ 30 дн.	6, 7
17	Дверь скрытого монтажа (короб под покраску) Д-5, проём 700×2100 мм, UNION FILO-60 / INVISIBLE ФИЛО-60, ГРУНТ; ИНВИЗИБЛ | FILO-60, FONDO; INVISIBLE	шт	1		1	1 шт	по запросу		≈ 30 дн.	6, 7
Черновые материалы — позиций 24, с ценой 2, итого 20 000 ₽										
Покрытия полов и облицовка										
18	Клей для паркетной и инженерной доски (эластичный, по ТУ изготовителя доски)	м²	43,18		43,18	фасовка по ТУ изделия	по запросу			2
Сухие смеси и гидроизоляция										
19	Клей плиточный цементный класса C2 TE S1 (ГОСТ Р 56387-2018) — Ceresit CM 17 или аналог	кг	209,32	10 %	230,25	10 мешок · мешок 25 кг	1 800 / меш.	18 000		8
20	Затирка цементная класса CG2WA, цвет — по колерной карте — Mapei Ultracolor Plus 132 или аналог	кг	2,62	10 %	2,88	2 упаковка · упак. 2 кг	1 000 / упак.	2 000		8
21	Гидроизоляция обмазочная полимерная, 2 слоя, лента в углах, манжеты на выводах	м²	11,29	10 %	12,42	фасовка по ТУ изделия	по запросу			2
22	Лента демпферная по периметру пола из плитки	м	15,39	10 %	16,93	17,00 м	по запросу			
23	Смесь цементно-песчаная для стяжки М200 (50 мм, 33 мм)	м³	2,77	5 %	2,91	фасовка по ТУ изделия	по запросу			2
24	Смесь штукатурная гипсовая для машинного и ручного нанесения по маякам, слой до 10 мм	м²	134,75	10 %	148,23	фасовка по ТУ изделия	по запросу			2
Короба из ГКЛВ										
25	Лист ГКЛВ 12,5 мм, 2500 × 1200 мм, обшивка коробов в 2 слоя	м²	3,52	10 %	3,87	2 лист · лист 3,00 м²	по запросу			
26	Профиль стальной оцинкованный 27 × 28 мм: каркас коробов (стойки и направляющие)	м	8,60	10 %	9,46	4 шт · хлыст 3 м	по запросу			

	Лист	№ док.	Подпись	Дата
Дизайнер	Кырлан А.С.			13.11.26
Проверил				
Н. контр.				
Утв.				

Проект: Квартира 56 м²

Смета материалов с ценами

Стадия	Лист	Листов
П	С8	92

Смета материалов с ценами (продолжение)

№	Позиция	Ед.	Нетто	Запас	С запасом	К закупке (упаковка)	Цена за ед., ₽	Сумма, ₽	Заказать заранее	Доп.
Перегородки и облицовки из ГКЛВ										
27	Лист ГКЛ 12,5 мм, 2500 × 1200 мм: обшивка перегородок и облицовок, 2 слоя на сторону	м²	21,36	10 %	23,50	8 лист · лист 3,00 м²	по запросу			
28	Профиль направляющий ПН 100: по потолку и полу, перемычки над проёмами	м	5,20	10 %	5,72	2 шт · хлыст 3 м	по запросу			
29	Профиль стоечный ПС 100: стойки через шаг каркаса и короткие над проёмами	м	11,40	10 %	12,54	5 шт · хлыст 3 м	по запросу			
30	Профиль усиленный УА 100 (2,0 мм): стойки по краям проёма на полную высоту	м	5,40	10 %	5,94	2 шт · хлыст 3 м	по запросу			
31	Плита минераловатная звукопоглощающая в полость каркаса, толщина по глубине профиля 100 мм	м²	5,34	10 %	5,87	фасовка по ТУ изделия	по запросу			2
32	Лента уплотнительная самоклеящаяся под профили по потолку, полу и у примыканий к стенам	м	9,80	10 %	10,78	11,00 м	по запросу			
33	Саморезы для ГКЛ по металлу (по слоям обшивки), дюбели для направляющих — по ТУ изготовителя системы	м²	21,36		21,36	фасовка по ТУ изделия	по запросу			2
Перегородки из кладки										
34	Пеноблок D500: изделия кладки толщиной 100 мм	м³	0,56		0,56	фасовка по ТУ изделия	по запросу			2
35	Смесь кладочная для блоков (клей или раствор — по виду изделия)	м³ кладки	0,56		0,56	фасовка по ТУ изделия	по запросу			2
36	Перемычка над проёмом в кладке П-1: L 1200 мм	шт	1		1	1 шт	по запросу			
37	Кирпич керамический полнотелый: изделия кладки толщиной 120 мм	м³	1,30		1,30	фасовка по ТУ изделия	по запросу			2
38	Смесь кладочная для кирпича (клей или раствор — по виду изделия)	м³ кладки	1,30		1,30	фасовка по ТУ изделия	по запросу			2
Лакокрасочные материалы										
39	Шпаклёвка финишная полимерная под окраску (стены и потолки, Q3)	м²	178,18	10 %	196,00	фасовка по ТУ изделия	по запросу			2
40	Грунтовка акриловая глубокого проникновения, 2 слоя	м²	201,80	10 %	221,98	фасовка по ТУ изделия	по запросу			2
Погонажные изделия и потолки										
41	Потолок подвесной ГКЛ/ГКЛВ по каркасу Knauf П113: листы, профили, подвесы, лента, шпаклёвка швов	м²	56,37		56,37	фасовка по ТУ изделия	по запросу			2
Электрика и слаботочные сети — позиций 40, с ценой 0, итого 0 ₽										
Слаботочные сети										
42	Кабель домофона — тип по системе поставщика	м	6,70		6,70	7,00 м	по запросу			3
43	Кабель коаксиальный RG-6 (75 Ом) к розеткам ТВ	м	11,70		11,70	12,00 м	по запросу			3
44	Кабель U/UTP кат. 6 (LAN, Wi-Fi и камеры по PoE)	м	44,90		44,90	45,00 м	по запросу			3
45	Гофротруба Ø20 для слаботочных линий, отдельно от силовых	м	57,00		57,00	57,00 м	по запросу			3
46	Розетка компьютерная RJ45, кат. 6, с рамкой и подрозетником	шт	3		3	3 шт	по запросу			
47	Розетка телевизионная (коаксиальная) с рамкой и подрозетником	шт	1		1	1 шт	по запросу			
48	Трубка или монитор домофона (поставка домофонной организации)	шт	1		1	1 шт	по запросу			
49	Щит слаботочный ЩС: корпус, DIN-рейка, розетки 220 В	шт	1		1	1 шт	по запросу			
50	Патч-панель, портов не менее 5	шт	1		1	1 шт	по запросу			
Электрика: силовая часть										
51	Кабель силовой ВВГнг(А)-LS 3×1,5 мм²	м	163,60		163,60	164,00 м	по запросу			3
52	Кабель силовой ВВГнг(А)-LS 3×2,5 мм²	м	186,10		186,10	187,00 м	по запросу			3
53	Кабель силовой ВВГнг(А)-LS 3×6 мм²	м	16,50		16,50	17,00 м	по запросу			3
Электрика: щит										
54	Автоматический выключатель дифференциального тока (АВДТ) C10 A, 30 мА, тип A	шт	4		4	4 шт	по запросу			4

	Лист	№ док.	Подпись	Дата
Дизайнер	Кырлан А.С.			13.11.26
Проверил				
Н. контр.				
Утв.				

Проект: Квартира 56 м²

Смета материалов с ценами (продолжение)	Стадия	Лист	Листов
	П	С9	92

выпуск 13.11.2026 № 568a382a0d · стр. 83 из 92

Смета материалов с ценами (продолжение)

№	Позиция	Ед.	Нетто	Запас	С запасом	К закупке (упаковка)	Цена за ед., ₽	Сумма, ₽	Заказать заранее	Доп.
55	Автоматический выключатель дифференциального тока (АВДТ) C16 A, 30 мА, тип A	шт	9		9	9 шт	по запросу			4
56	Автоматический выключатель дифференциального тока (АВДТ) C32 A, 30 мА, тип A	шт	1		1	1 шт	по запросу			4
57	Корпус щита ЩРВ-П-48, IP41, 48 модулей	шт	1		1	1 шт	по запросу			4
58	Вводной автомат C50, 1P+N	шт	1		1	1 шт	по запросу			4
59	Вводное УЗО-А 63 А, 100 мА (селективное)	шт	1		1	1 шт	по запросу			4
60	УЗИП тип 2	шт	1		1	1 шт	по запросу			4
Электрика: механизмы и изделия										
61	Розетка с з/к и защитными шторками, 16 А	шт	34		34	34 шт	по запросу			4
62	Розетка IP44 с крышкой, 16 А	шт	2		2	2 шт	по запросу			4
63	Выключатель 1-клав.	шт	1		1	1 шт	по запросу			4
64	Выключатель 1-клав. проходной	шт	1		1	1 шт	по запросу			4
65	Выключатель 2-клав.	шт	1		1	1 шт	по запросу			4
66	Выключатель 2-клав. (перекрёстная + проходная)	шт	1		1	1 шт	по запросу			4
67	Выключатель 2-клав. (проходная + обычная)	шт	4		4	4 шт	по запросу			4
68	Выключатель 2-клав. проходной	шт	1		1	1 шт	по запросу			4
69	Светорегулятор 1-канальный, задний фронт (LED)	шт	4		4	4 шт	по запросу			4
70	Датчик движения ночной подсветки	шт	1		1	1 шт	по запросу			4
71	Рамка 1-постовая	шт	37		37	37 шт	по запросу			4
72	Рамка 2-постовая	шт	6		6	6 шт	по запросу			4
73	Коробка установочная (подрозетник) Ø68	шт	49		49	49 шт	по запросу			4
74	Вывод кабеля под прибор (клеммник)	шт	5		5	5 шт	по запросу			4
75	Коробка уравнивания потенциалов КУП	шт	1		1	1 шт	по запросу			4
76	Блок питания LED 24 В, 300 Вт, дим.	шт	1		1	1 шт	по запросу			4
77	Блок питания LED 24 В, 60 Вт, дим.	шт	1		1	1 шт	по запросу			4
78	Блок питания LED 24 В, 200 Вт, дим.	шт	2		2	2 шт	по запросу			4
79	Блок питания LED 24 В, 20 Вт	шт	1		1	1 шт	по запросу			4
80	Извещатель дымовой автономный	шт	3		3	3 шт	по запросу			4
81	Извещатель тепловой	шт	2		2	2 шт	по запросу			4
Сантехника — позиций 32, с ценой 0, итого 0 ₽										
Сантехника: санитарные приборы										
82	Ванна встраиваемая акриловая 1700×750 мм, с каркасом, экраном и отверстием слив-перелив — акриловая 1700×750, смеситель настенный	шт	1		1	1 шт	по запросу			5
83	Унитаз подвесной безободковый, с сиденьем микролифт, крепёж и звукоизолирующая прокладка — Laufen Pro 8.2096.6.000.000.1	шт	1		1	1 шт	по запросу			5
84	Инсталляция для подвесного унитаза: рама высотой 1120 мм, бачок, клавиша смыва (ось клавиши 1050 мм от чистого пола)	шт	1		1	1 шт	по запросу			5, 1
85	Раковина над стиральной машиной 600×450 мм, плоская, с переливом и выпуском под плоский сифон	шт	1		1	1 шт	по запросу			5, 1
86	Мойка врезная, нержавеющая сталь, чёрная 700×480 мм, с переливом	шт	1		1	1 шт	по запросу			5, 1
87	Полотенцесушитель электрический, IP44, с терморегулятором	шт	1		1	1 шт	по запросу			5, 1
Сантехника: смесители, сифоны и арматура приборов										
88	Смеситель для ванны настенный однорычажный, межосевое 150 мм, с душевым набором (лейка, шланг, держатель)	шт	1		1	1 шт	по запросу			5, 1

	Лист	№ док.	Подпись	Дата
Дизайнер	Кырлан А.С.			13.11.26
Проверил				
Н. контр.				
Утв.				

Проект: Квартира 56 м²

Смета материалов с ценами (продолжение)	Стадия	Лист	Листов
	П	С10	92

выпуск 13.11.2026 № 568a382a0d · стр. 84 из 92

Смета материалов с ценами (продолжение)

№	Позиция	Ед.	Нетто	Запас	С запасом	К закупке (упаковка)	Цена за ед., ₽	Сумма, ₽	Заказать заранее	Доп.
89	Смеситель для умывальника однорычажный, с донным клапаном	шт	1		1	1 шт	по запросу			5, 1
90	Смеситель кухонный однорычажный, высокий излив	шт	1		1	1 шт	по запросу			5, 1
91	Обвязка ванны слив-перелив Ø40/50 с сифоном	шт	1		1	1 шт	по запросу			5, 1
92	Сифон плоский для раковины над стиральной машиной Ø32/40–50, выпуск в стену над корпусом машины	шт	1		1	1 шт	по запросу			5, 1
93	Сифон для мойки с отводом для ПММ Ø40/50	шт	1		1	1 шт	по запросу			5, 1
94	Сифон для стиральной машины встраиваемый в стену Ø50, с обратным клапаном	шт	1		1	1 шт	по запросу			5, 1
95	Кран угловой ½"×½" с гибкой подводкой 40 см (умывальники, мойка)	шт	4		4	4 шт	по запросу			5, 1
96	Кран шаровой угловой ½"×¾" для подключения стиральной и посудомоечной машины	шт	2		2	2 шт	по запросу			5, 1
Сантехника: трубопроводы										
97	Труба полипропиленовая PP-R PN20 Ø20×3,4 (B1) — ГОСТ 32415-2013	м	21,50	10 %	21,50	21,50 м	по запросу			5
98	Труба PP-R, армированная стекловолокном, PN20 Ø20×2,8 (T3) — ГОСТ 32415-2013	м	19,00	10 %	19,00	19,00 м	по запросу			5
99	Труба канализационная ПП Ø50 (К1) — ГОСТ 32414-2013	м	24,00	10 %	24,00	24,00 м	по запросу			5
100	Труба канализационная ПП Ø110 (К1) — ГОСТ 32414-2013	м	1,00	10 %	1,00	1,00 м	по запросу			5
Сантехника: фасонные части и выводы										
101	Отвод канализационный ПП 45° Ø50 — ГОСТ 32414-2013	шт	16		16	16 шт	по запросу			5
102	Отвод канализационный ПП 45° Ø110 — ГОСТ 32414-2013	шт	4		4	4 шт	по запросу			5
103	Тройник канализационный ПП 45° (врезки ветвей) — ГОСТ 32414-2013	шт	4		4	4 шт	по запросу			5
104	Ревизия канализационная ПП (после поворота трассы) — ГОСТ 32414-2013	шт	6		6	6 шт	по запросу			5
105	Фитинги PP-R Ø20: тройники, угольники 90° (ветви и повороты B1, T3) — ГОСТ 32415-2013	шт	23		23	23 шт	по запросу			5
106	Водорозетка PP-R Ø20×½" настенная, с креплением — ГОСТ 32415-2013	шт	9		9	9 шт	по запросу			5
Сантехника: узлы ввода, люки, короба										
107	Кран шаровой латунный Ду15 PN16 (отключение ввода)	шт	2		2	2 шт	по запросу			5, 1
108	Фильтр сетчатый косой Ду15	шт	2		2	2 шт	по запросу			5, 1
109	Счётчик воды крыльчатый Ду15 (ХВ, ГВ), с поверкой	шт	2		2	2 шт	по запросу			5, 1
110	Клапан обратный Ду15	шт	2		2	2 шт	по запросу			5, 1
111	Люк ревизионный нажимной под плитку 300×400 мм	шт	1		1	1 шт	по запросу			5, 1
112	Звукоизоляция стояка К1 в коробе: рулонный звукоизоляционный материал ≥ 10 мм, обмотка стояка на высоту этажа	м	2,70		2,70	2,70 м	по запросу			5, 1
113	Короб К1 над полом: профиль ПН/ПС, ГКЛВ 12,5 мм под плитку	м	9,70		9,70	9,70 м	по запросу			5, 1
	ИТОГО материалы (позиций с ценой 14 из 113; без цены 99 — «по запросу», в итог не входят)							**497 009**		

Примечания

1. Количества — из единой книги материалов проекта: тот же расход, что в спецификации отделочных материалов, смете и списке покупок. Запас — на подрезку и бой; норма запаса печатается в графе «Запас», её основание — в отдельном документе «Смета на материалы».
2. Цены — нижняя граница открытых прайсов (прайсы собраны 21.09.2026, часть расценок сверена повторно 06.10.2026 и 08.11.2026, Москва); не предложение (оферта) магазинов. Цены нет — «по запросу», позиция в итог не входит. Работы в эту смету не входят (они — на листе «Смета проекта»).
3. Доп. 1. Изделие не выбрано: позиция описана по характеристикам («аналог»); марка, артикул и цена определяются при выборе изделия.
4. Доп. 2. Фасовка не задана в данных: количество дано в мерах расчёта, число упаковок определяется по выбранному продукту (расход и тара — по ТУ).
5. Доп. 3. Длина кабеля — по длинам групп щита из данных электрика; запас на подрезку в длину не заложен — берите бухту с запасом 5–10 %.
6. Доп. 4. Механизмы, рамки и подрозетники — по ведомости изделий электрика; серию механизмов выбирает заказчик.
7. Доп. 5. Трубы и фасонные части — по трассам листа разводки, +10 % на подрезку (уже в количестве); модели приборов заказчик выбирает сам.
8. Доп. 6. Двери: цена и срок называет поставщик после выбора изделия; в смету стоят только если цена задана в данных.
9. Доп. 7. Срок поставки — из данных проекта; если срок не задан, указан типовой диапазон практики как ориентир, а не срок поставщика.
10. Доп. 8. Цена — нижняя граница открытых прайс-листов на дату сбора (книга цен проекта); не коммерческое предложение магазина.
11. Доп. 9. Доли по помещениям справочные: общая закупка делится пропорционально площади (длине, числу), по которой считается позиция.

	Лист	№ док.	Подпись	Дата
Дизайнер	Кырлан А.С.			13.11.26
Проверил				
Н. контр.				
Утв.				


Проект: Квартира 56 м²

Смета материалов с ценами (окончание)

Стадия	Лист	Листов
П	С11	92

1 Порог 15 мм: мокрая зона — смежное помещение (М 1:5)


Применение: двери Д-5

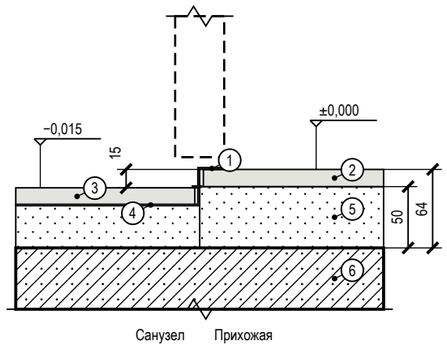

Поз.	Состав слоя, изделие
1	порог-переход металлический, перепад 15 мм, на клей-герметик
2	керамогранит на клею С2 TE S1
3	керамогранит на клею С2 TE S1
4	гидроизоляция в 2 слоя с подъёмом на торец ступени, лента в углу
5	ЦПС М200 50 мм; в мокрой зоне 33 мм
6	плита перекрытия

2 Стык покрытий пола Т-профилем без перепада (М 1:5)

Применение: проёмы 1↔5, 2↔5, 3↔5

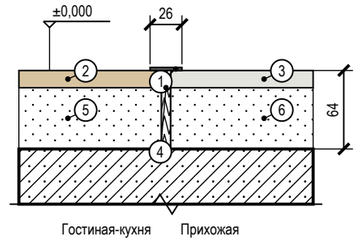

Поз.	Состав слоя, изделие
1	Т-профиль алюминиевый, полка 26 мм, ножка в шов; цвет — по покрытию
2	Гостиная-кухня: инженерная доска на клею
3	Прихожая: керамогранит на клею С2 TE S1
4	шов 8 мм по оси полотна двери, заполнитель эластичный
5	Гостиная-кухня: стяжка ЦПС М200 50 мм
6	Прихожая: стяжка ЦПС М200 50 мм

3 Дверь скрытого монтажа в плоскости стены, плинтус (М 1:5)

Применение: двери Д-2, Д-3, Д-4, Д-5

Поз.	Состав слоя, изделие
1	плинтус МДФ 80×16 на клей; у короба — зазор 5 мм, окраска в цвет стены
2	полотно 40 мм под окраску, заподлицо со стеной; теневой шов 3 мм
3	стена 150 мм, штукатурка 10 мм с двух сторон
4	короб скрытого монтажа (алюминий), лицом в плоскости отделки; монтаж до штукатурки

4 Короб стояков К1-1 с люком и звукоизоляцией (М 1:10)

Применение: пом. 4

Поз.	Состав слоя, изделие
1	стены существующие — не ослаблять
2	короб: профиль 27×28, ГКЛВ 2×12,5 мм, облицовка плиткой
3	звукоизоляция стояков рулонная 20 мм; К1-1 Ø110
4	ревизионный люк 300×400 мм нажимной, под плитку; против ревизии стояка

Условные обозначения

- железобетон (плита, стены) — условно: конструкция не установлена
- кладка, перегородка — условно: конструкция не установлена
- стяжка, раствор
- гипсокартон ГКЛВ
- звукоизоляция, эластичный заполнитель
- плитка, керамогранит на клею
- инженерная доска (покрытие пола)
- металлический профиль (порог, Т-профиль, короб двери)
- гидроизоляция (обмазочная, лента)

Примечания

1. Узлы — типовые решения проекта для мест, отмеченных выносками на листе схемы расположения развёрток и узлов; размеры — в мм, отметки — в м от ±0,000.
2. Узлы с гидроизоляцией, закладными и коробами скрытого монтажа принимаются по актам скрытых работ до закрытия отделкой; гидроизоляция — после теста проливом (24 ч).
3. Марки изделий (порог, Т-профиль, короб скрытой двери, люк) — по спецификациям; замена — на аналог с теми же габаритами по согласованию с автором проекта.
4. Материал плиты перекрытия и стен в узлах показан условно (железобетон, кладка): конструкция дома не установлена — крепёж, анкеры и толщины слоёв уточняются после обследования (до него — по допущениям общих указаний).
5. Узлы комплекта выпущены на 2 листах, нумерация узлов сквозная: 1–4 — лист С12 альбома (данный лист); 5–7 — лист С13 альбома.

	Лист	№ док.	Подпись	Дата
Дизайнер	Кырлан А.С.			13.11.26
Проверил				
Н. контр.				
Утв.				


Проект: Квартира 56 м²

Узлы. Лист 1 из 2	Стадия	Лист	Листов
	П	С12	92

выпуск 13.11.2026 № 568a382a0d · стр. 86 из 92

5 Гидроизоляция санузла: заход на стены 200 мм, примыкание ванны (М 1:10)


Применение: пом. 4

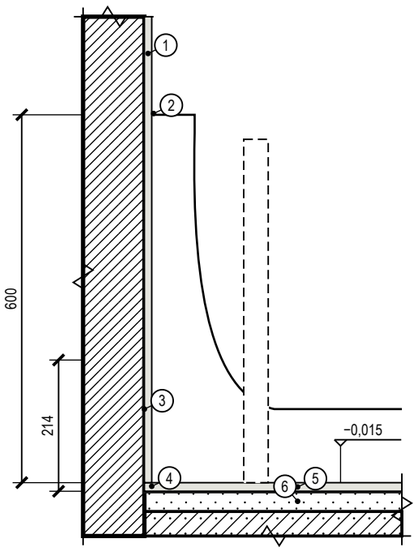

Поз.	Состав слоя, изделие
1	облицовка — плитка на клею С2 TE S1, затирка CG2WA
2	примыкание ванны: лента бордюрная + силиконовый санитарный герметик; облицовка опирается на борт
3	гидроизоляция обмазочная в 2 слоя, заход на стены 200 мм (в зоне душа выше), до облицовки; акт скрытых работ, тест проливом
4	лента гидроизоляционная в углах и у трапов
5	керамогранит на клею С2 TE S1
6	ЦПС М200 33 мм

6 Плинтус МДФ 80×16 мм у окрашенной стены по доске (ламинату) (М 1:5)


Применение: пом. 1, 2, 3

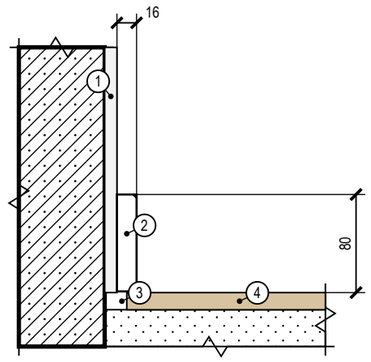

Поз.	Состав слоя, изделие
1	штукатурка, шпаклёвка Q3, окраска — по ведомости отделки
2	плинтус МДФ 80×16 под окраску в цвет стены; клей монтажный — к стене, не к полу
3	зазор покрытия у стены 8–10 мм закрывается плинтусом
4	инженерная доска на клею

7 Плинтус МДФ 80×16 мм у окрашенной стены по керамограниту (плитке) (М 1:5)

Применение: пом. 5

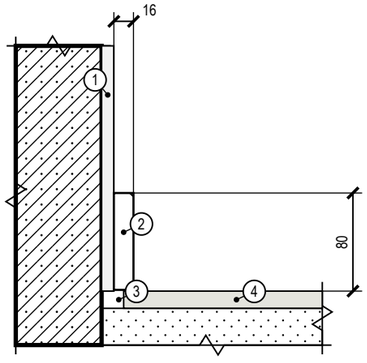

Поз.	Состав слоя, изделие
1	штукатурка, шпаклёвка Q3, окраска — по ведомости отделки
2	плинтус МДФ 80×16 под окраску в цвет стены; клей монтажный — к стене, не к полу
3	зазор покрытия у стены 8–10 мм закрывается плинтусом
4	керамогранит на клею С2 TE S1

Условные обозначения

- железобетон (плита, стены) — условно: конструкция не установлена
- кладка, перегородка — условно: конструкция не установлена
- стяжка, раствор
- плитка, керамогранит на клею
- инженерная доска (покрытие пола)
- гидроизоляция (обмазочная, лента)


Примечания

1. Узлы — типовые решения проекта для мест, отмеченных выносками на листе схемы расположения развёрток и узлов; размеры — в мм, отметки — в м от ±0,000.
2. Узлы с гидроизоляцией, закладными и коробами скрытого монтажа принимаются по актам скрытых работ до закрытия отделкой; гидроизоляция — после теста проливом (24 ч).
3. Марки изделий (порог, Т-профиль, короб скрытой двери, люк) — по спецификациям; замена — на аналог с теми же габаритами по согласованию с автором проекта.
4. Материал плиты перекрытия и стен в узлах показан условно (железобетон, кладка): конструкция дома не установлена — крепёж, анкеры и толщины слоёв уточняются после обследования (до него — по допущениям общих указаний).
5. Узлы комплекта выпущены на 2 листах, нумерация узлов сквозная: 1–4 — лист С12 альбома; 5–7 — лист С13 альбома (данный лист).

	Лист	№ док.	Подпись	Дата	Проект: Квартира 56 м²			
Дизайнер	Кырлан А.С.			13.11.26				
Проверил					Узлы. Лист 2 из 2	Стадия	Лист	Листов
Н. контр.								
Утв.						П	С13	92

выпуск 13.11.2026 № 568a382a0d · стр. 87 из 92

№	Работа	Нед.	После
Р-1	**демонтаж**	1	
Р-2	**контрольный обмер**	0,5	Р-1
Р-3	**перегородки**	0,75	Р-2
Р-4	**черновая электрика**	1,25	Р-3, Р-2
Р-5	черновая сантехника	1	Р-3, Р-2
Р-6	**штукатурка**	2	Р-4, Р-5, Р-3
Р-7	**стяжка**	0,75	Р-6
Р-8	**гидроизоляция**	0,5	Р-7
Р-9	ГКЛ	1,25	Р-4, Р-5
Р-10	**плитка**	2,75	Р-8, Р-9, Р-7
Р-11	**шпаклёвка**	2,25	Р-10, Р-9, Р-6
Р-12	**окраска**	1,75	Р-11
Р-13	**чистовые полы**	1	Р-12, Р-10
Р-14	**двери и плинтусы**	0,75	Р-13, Р-12
Р-15	**чистовая электрика и сантехника**	0,75	Р-14, Р-12
Р-16	**кухня и мебель**	0,75	Р-15, Р-14
Р-17	**сдача**	0,5	Р-16, Р-15
Закупки: заказать не позднее — «◆»; от заказа до поставки — штриховая полоса; срок поставки — только из данных или «ориентир практики»			
З-1	Двери скрытого монтажа с коробом под покраску в новой перегородке П-2: Д-4 — 1 шт.	4,25	для Р-3
З-2	Двери скрытого монтажа с коробом под покраску в существующих проёмах: Д-2, Д-3, Д-5 — 3 шт	4,25	для Р-6
З-3	Кухонный гарнитур по проекту кухни: модули М-01, М-02, М-03, М-04, М-05, М-06, М-07, М-08,	6	для Р-16
З-4	Встраиваемая техника кухни: М-01 холодильник, М-06 посудомоечная машина, М-08 вытяжка		для Р-16
З-5	Стиральная машина: ОБ-03 (вертикальная загрузка 400 × 600 мм — условие закупки)		для Р-5
З-6	Сантехнические приборы и инсталляции: С-01, С-02, С-03, С-04		для Р-5
З-7	Керамогранит и плитка: 3 поз. по артикулу и формату, 35,94 м² по раскладке		для Р-10
З-8	Покрытие пола (доска) и плинтус: пом. 1, 2, 3		для Р-13
З-9	Встроенная мебель по замеру цеха: М-19, М-23, М-27	6	для Р-16

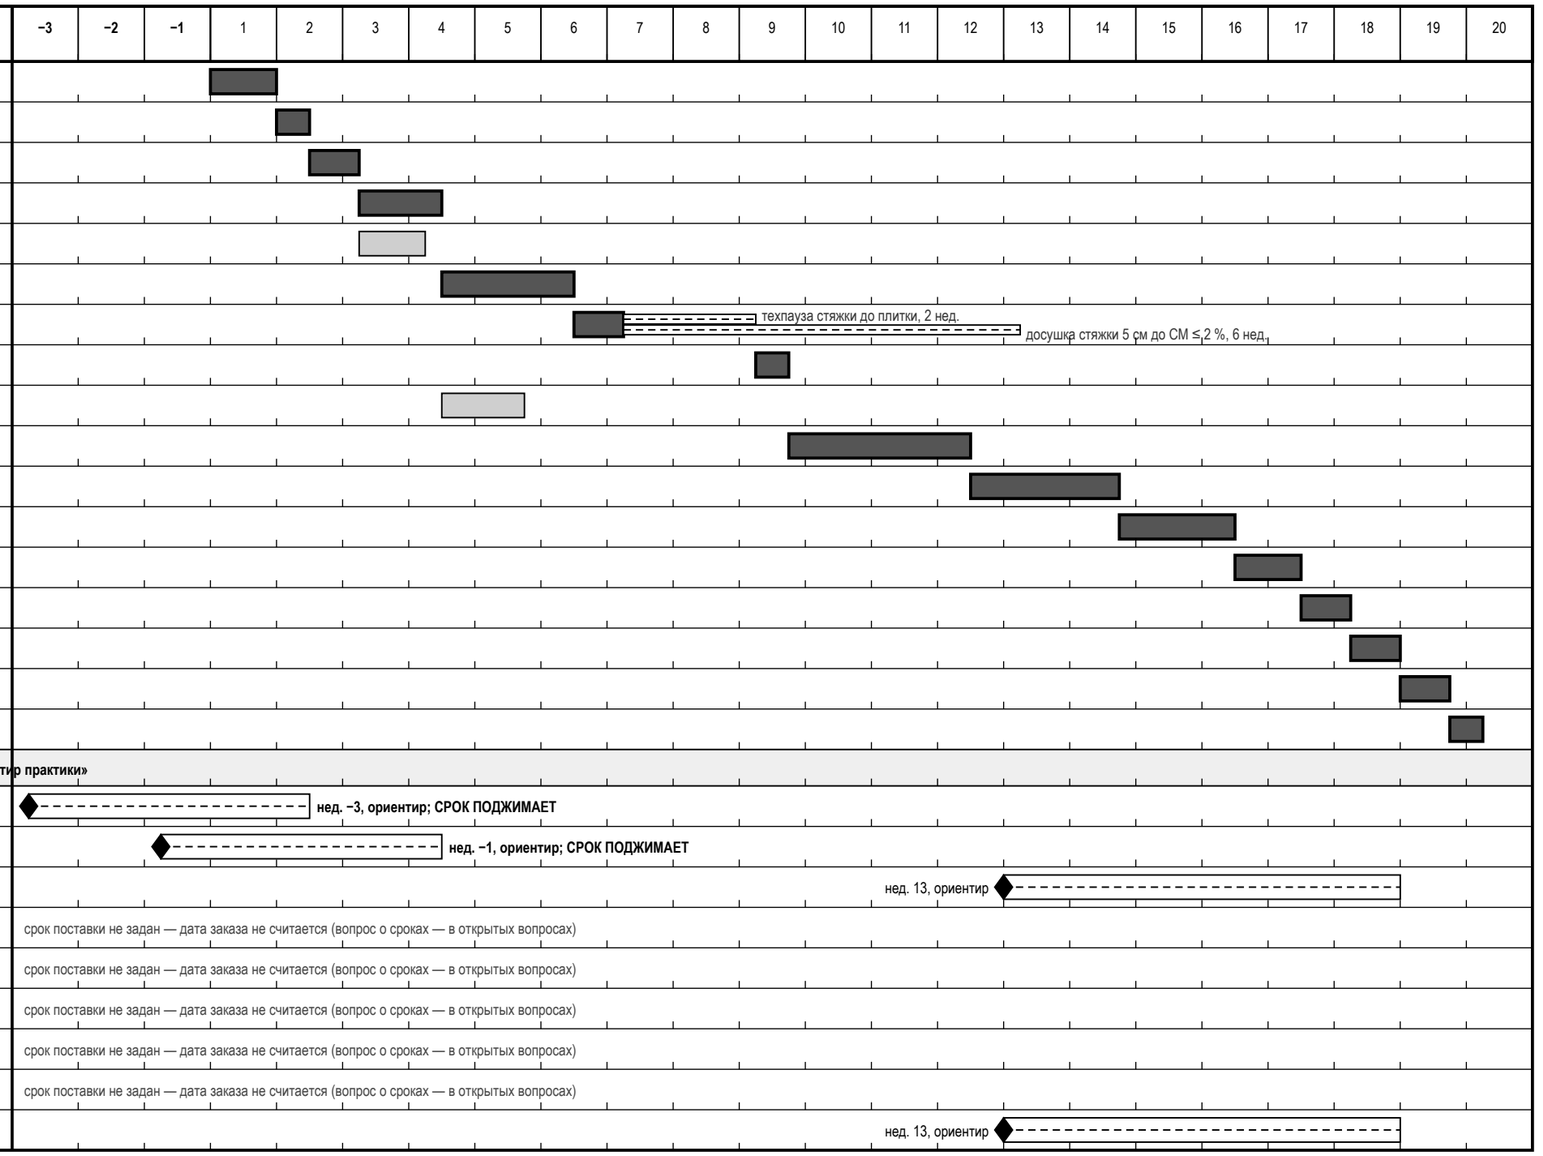

Итого: ≈ 19,25 нед. · жирная линия и тёмная полоса — критический путь

Примечания

1. Длительности этапов — типовые сроки по площади 56,37 м² (таблица «Свод для графика»: недели по этапам для 45, 80 и 120 м², середина вилки, линейная интерполяция); это ориентир, а не норма и не обещание бригады. Контрольный обмер — ориентир 0,5 нед. (в таблице нет).
2. Зависимости «после» — из графика закупок и работ (лист «График закупок и работ»); каждая работа начинается после конца предшественников. Техпаузы стоят отдельными полосами, а не спрятаны в длительности: стяжка → плитка — не менее 2 нед.; стяжка → чистовой пол — досушка стяжки 5 см до СМ ≤ 2 % — 6 нед. (ориентир «1 нед. на 1 см до 4 см, 5 см — 6 нед., 6 см — 8 нед.»; решает замер).
3. График последовательный и поэтому консервативный: в жизни шпаклёвка, плитка и досушка стяжки идут частично параллельно (таблица типовых сроков для 56,37 м²: 13–17 нед.). Совмещения — решение прораба после обмера.
4. Закупки: «заказать не позднее» = начало работы, которой нужна позиция, минус срок поставки. Срок поставки — из данных проекта (срок поставки позиции, срок изготовления обоев в отделке); если его нет, в графике стоит типовой диапазон практики с пометкой «ориентир» — это не срок поставщика, его надо получить до заказа. Кухню и встроенную мебель заказывают после замера по готовым стенам (после штукатурки). Позиции без срока дат заказа не имеют.
5. «Срок поджимает»: самая поздняя дата заказа раньше, чем позицию можно заказать (до замера или обмера): сдвиньте начало работ, ищите изделие с меньшим сроком или заказывайте по предварительному размеру — решение прораба и заказчика.

	Лист	№ док.	Подпись	Дата
Дизайнер	Кырлан А.С.			13.11.26
Проверил				
Н. контр.				
Утв.				

Проект: Квартира 56 м²

Календарный график работ и закупок	Стадия	Лист	Листов
	П	С14	92

выпуск 13.11.2026 № 568a382a0d · стр. 88 из 92

Приёмка по этапам: контрольные точки, допуски и акты скрытых работ

Этап	Контрольная точка (дальше не пускают без подписи)	Что проверяют	Чем	Допуск	Основание	Подпись	Акт скрытых работ / документ
Р-1	Демонтаж До начала демонтажа: запрошены документы на дом и БТИ	Что снимается и что не трогается: покрытия, отделка, дверные блоки; несущие стены и перегородки — без изменений	осмотр по плану демонтажа	снятое — только по плану; несущее не затрагивать	практика		Фото помещений до и после демонтажа; перечень снятого в журнале работ.
Р-2	Контрольный обмер Контрольный обмер на голых стенах сделан до заказа всего, что делают по размеру	Размеры помещений и проёмов, диагонали, положение стояков, щитка, каналов, толщины стен	рулетка, лазерный дальномер, уровень	допуск задаёт проект; расхождение с планом — в перечень открытых вопросов до заказа	практика		Протокол контрольного обмера с эскизом; расхождения занесены в открытые вопросы.
Р-3	Перегородки Перегородки: разметка против плана монтажа подписана до обшивки	Шаг саморезов: потолок 150 мм; стена 200 мм (лист вертикально) или 300 мм (горизонтально)	рулетка	150 / 200 / 300 мм	практика (СП 163.1325800.2014)		Акт скрытых работ: каркас ГКЛ, закладные под тяжёлое, звукоизоляция в перегородках — до обшивки (фото закладных с привязками); армирование и примыкание к несущим.
		Отступ самореза от кромки и угла листа; расстояние между саморезами на стыке листов	рулетка	5–10 мм от кромки; не менее 15 мм на стыке	практика (СП 163.1325800.2014)		
		Заделка стыков: лента и не менее 2 слоёв шпаклёвки; шляпки утоплены вровень, без прорыва картона	визуально, на просвет	без трещин после высыхания	практика		
		Прогиб каркаса: нет люфта между листом и профилем	простукивание, нажатие рукой	точной цифры нет — сверить перед актом	практика		
Р-4	Черновая электрика Черновая электрика: трассы, высоты подрозетников, замер изоляции подписаны до заделки	Сопротивление изоляции проводки (цепи до 1000 В)	мегаомметр	не менее 0,5 МОм	норматив (ПУЭ, гл. 1.8)		Акт скрытых работ на трассы проводки и слаботочные линии до закрытия штукатуркой и ГКЛ; исполнительная схема трасс с привязками; заземление и уравнивание потенциалов в санузле протокол и фото.
		Целостность и маркировка: PE жёлто-зелёный, N — синий, L — прочие цвета	визуально, прозвонка	каждый проводник промаркирован	практика		
		Высоты подрозетников и привязки — по плану розеток и выключателей	рулетка, уровень	по проекту; от чистого пола	практика		
Р-5	Черновая сантехника Черновая сантехника: опрессовка, отметки выводов, инсталляции подписаны до зашивки	Опрессовка водоснабжения: рабочее давление до 0,6 МПа — испытание 0,9 МПа; выше 0,6 МПа — по расчёту	опрессовочный насос, манометр	выдержка 10 мин (поквартирная); падение: пластик не более 0,06 МПа за 30 мин, сталь не более 0,05 МПа за 10 мин	практика (СП 73.13330)		Акт опрессовки (давление, время, результат); акт скрытых работ на трассы в стенах, полу и коробах; инсталляции, скрытые смесители, трапы — фото с рулеткой и отметками.
		Уклон канализации Ø40–50	уровень, построитель плоскостей	не менее 20 мм на 1 м	норматив (СП 30.13330)		
		Протечки в соединениях, сифоны, смесители, гибкая подводка	осмотр под давлением, салфетка на стыках	нет капель и влажных следов в контрольное время	практика		
		Отметки выводов и положение инсталляций до зашивки и гидроизоляции	рулетка в кадре, фото	по листу выводов	практика		
Р-6	Штукатурка Маяки стен проверены до штукатурки; коробки скрытых дверей стоят до штукатурки	Отклонение от вертикали (простая / улучшенная / высококачественная штукатурка)	отвес, лазерный уровень	3 / 2 / 1 мм на 1 м; не более 15 / 10 / 5 мм на высоту	практика (СП 71.13330.2017)		Фото коробок скрытых дверей с отметкой чистого пола — до штукатурки; класс штукатурки (простая / улучшенная / высококачественная) назван в договоре.
		Отклонение от горизонтали	уровень, правило	3 / 2 / 1 мм на 1 м; не более 15 / 10 / 5 мм на длину	практика (СП 71.13330.2017)		
		Неровности (плоскостность)	правило 2 м и щуп	до 5 / 3 / 2 мм на 1 м; не более 3 / 2 / 2 неровностей на 4 м²	практика (СП 71.13330.2017)		
		Влажность основания перед шпаклёвкой и отделкой	влагомер	верхние 20–30 мм — не более 5 % по массе	норматив (СП 71, табл. 7.2)		

	Лист	№ док.	Подпись	Дата	Проект: Квартира 56 м²			
Дизайнер	Кырлан А.С.			13.11.26				
Проверил					Чек-лист приёмки по этапам. Лист 1 из 3	Стадия	Лист	Листов
Н. контр.						П	С15	92
Утв.								

выпуск 13.11.2026 № 568a382a0d · стр. 89 из 92

Приёмка по этапам: контрольные точки, допуски и акты скрытых работ (продолжение)

Этап	Контрольная точка (дальше не пускают без подписи)	Что проверяют	Чем	Допуск	Основание	Подпись	Акт скрытых работ / документ
Р-7	Стяжка Стяжка: подготовка, после заливки ровность, затем замер СМ перед чистовым полом	Ровность: просвет под рейкой 2 м	рейка 2 м, клиновой щуп	под паркет, ламинат — 2 мм; под гидроизоляцию до 4 мм; прочие покрытия — до 6 мм (цифры расходятся между источниками — сверить перед актом)	практика (СП 29.13330)		Акт скрытых работ на стяжку (толщина, армирование) до чистового пола; протокол ровности и протокол СМ-влажности; звукоизоляция и демпферная лента под стяжкой — фото и паспорт; контуры тёплого пола до заливки — схема укладки и замер сопротивления.
		Отклонение от горизонтали по помещению	уровень, нивелир	не более 0,2 % длины помещения	практика (СП 29.13330)		
		Число точек измерения	рейка	не менее 3 на 30 м² или 1 на небольшое помещение	практика		
		Отслоения и пустоты	простукивание молотком или киянкой	глухой звук — зона вскрывается и переделывается	практика		
		Влажность перед укладкой доски: цементная стяжка	влагомер; СМ-замер	ЦПС не более 2,0 % СМ (с тёплым полом не более 1,8 %); влагомер для плитки — не более 5 %	практика (СП 71; рекомендации производителей)		
Р-8	Гидроизоляция Гидроизоляция: пролив 24 ч подпись до плитки	Заведение на стены не ниже 200 мм от чистого пола; за ванной — 300 мм выше борта; в душе без поддона — на высоту лейки	рулетка	не менее 200 мм	норматив (СП 71.13330.2017, п. 8.6.5); остальное — практика		Акт теста проливом, фото узлов и высоты заведения на стены — до плитки.
		Тест проливом: слой воды 10–30 мм, контроль уровня и потолка соседа снизу	линейка, визуально	24 ч (минимум 12 ч); падения уровня и протечки нет	практика		
		Два слоя обмазки с межслойной сушкой, лента в углах и манжеты на выводах	визуально	по инструкции производителя	практика		
Р-9	ГКЛ Короба, ниши и потолки: черновые сети в зоне коробов приняты до обшивки	Шаг саморезов, отступ от кромки, заделка стыков (как у перегородок)	рулетка, визуально	потолок 150 мм; кромка 5–10 мм; стык — лента и 2 слоя шпаклёвки	практика (СП 163.1325800.2014)		Акт скрытых работ: каркас ГКЛ, закладные, звукоизоляция — фото до обшивки; воздуховоды в коробах и за потолком — фото и схема.
		Закладные под тяжёлое, карнизы, подвесные светильники на месте до обшивки	фото с привязками	по плану потолков и узлам	практика		
		Ревизионные люки: доступ к арматуре и ревизиям сохранён	осмотр	по листу ВК	практика		
Р-10	Плитка Раскладка плитки: первая плита и первый ряд проверены по развёртке; плитка выбрана, калибр партии измерен	Уступы между смежными плитками	линейка, на просвет	не более 1 мм	норматив (СП 71.13330.2017)		Раскладка подписана до начала плитки; протокол первого ряда; акт теста проливом приложен (этап гидроизоляции).
		Ширина шва и его прямолинейность	линейка, калибр	до 6 мм ручная укладка; фактическая по проекту ±0,5 мм	практика		
		Отклонение рядов от вертикали и горизонтали	уровень, правило, отвес	1,5 мм на 1 м длины	практика		
		Ровность облицовки	правило 2 м и щуп	не более 2–4 мм (цифра расходится по источникам)	практика		
		Пустоты под плиткой	простукивание всей площади	до 10 % площади допустимо; свыше 25 % под одной плиткой — брак	практика		
Р-11	Шпаклёвка Шпаклёвка Q3/Q4: проверка боковым светом до окраски	Класс основания под окраску: Q3 — сплошное финишное шпаклевание; Q4 — под направленный свет	переносной прожектор у поверхности под острым углом	Q3: царапины от абразива до 0,5 мм; Q4 — без видимых царапин и теней; неровность на 2 м: Q3 — 1 мм, Q4 — 0,5 мм	практика (Q-классы — не норматив СП, а согласованный критерий)		Класс (Q3 или Q4) назван в договоре; грунтование и армирование стыков перед шпаклёвкой — запись в журнале.
Р-12	Окраска Выкрасы утверждены, колеровка одной партией	Окраска без полос, подтёков, пропусков; цвет — по колерной карте	боковой свет, образец выкраса	без видимых дефектов при боковом свете	практика		Утверждённые выкрасы; остаток колеровки одной партии — для подкраски.

	Лист	№ док.	Подпись	Дата
Дизайнер	Кырлан А.С.			13.11.26
Проверил				
Н. контр.				
Утв.				

Проект: Квартира 56 м²

Чек-лист приёмки по этапам. Лист 2 из 3	Стадия	Лист	Листов
	П	С16	92

Приёмка по этапам: контрольные точки, допуски и акты скрытых работ (продолжение)

Этап	Контрольная точка (дальше не пускают без подписи)	Что проверяют	Чем	Допуск	Основание	Подпись	Акт скрытых работ / документ
		Основание сухое, огрунтованное; защита от прямого солнца при высыхании	осмотр	по ТУ краски	норматив (СП 71.13330.2017, п. 7.5.2)		
Р-13	Чистовые полы Чистовые полы: влажность, ровность, уступы, зазоры — до укладки доски; мокрые работы закончены	Деформационный зазор у стен и порогов (доска, ламинат)	линейка, клинья при укладке	8–15 мм (чаще 10 мм); у ламината 5–10 мм по СП 71	практика (требования производителей); норматив (СП 71, п. 8.10.14)		Протокол СМ-влажности стяжки до укладки; паспорт и партия доски.
		Перепад основания под покрытие	правило 2 м и щуп	не более 2 мм на 2 м	практика		
		Зазоры и перепады между досками; скрип; видимый зазор в замке — брак	щуп, рука, шаг	«ступеньки» нет	практика		
		Влажность помещения при укладке и после	гигрометр	не более 60 %, без сквозняков	норматив (СП 71, п. 8.1.7)		
Р-14	Двери и плинтусы Полотна и плинтусы — после чистового пола; скрытые полотна после чистовой отделки стен	Отклонение коробки от вертикали	отвес, уровень	1,5 мм на 1 м, не более 3 мм на коробку	практика (ТР 105-00, пересказ)		Коробки скрытых дверей приняты до штукатурки (этап штукатурки); паспорт на полотна.
		Зазор между полотном и коробкой по периметру	щуп	2–4 мм по бокам и верху (единого норматива нет)	практика		
		Открывание и закрывание: без перекоса, плавный ход петель и доводчика	визуально, от руки	без задевания коробки и пола	практика		
Р-15	Чистовая электрика и сантехника Чистовая электрика и сантехника: протокол электролаборатории и проверка УЗО до подписи акта	УЗО: кнопка «Тест»; время отключения; ток отключения	кнопка на аппарате; прибор проверки УЗО (не мультиметр)	отключает; не более 0,3 с; 50–100 % от IΔn	практика измерений		Протокол измерений аккредитованной электролаборатории (изоляция по группам, УЗО, PE, фаза-ноль); исполнительная схема щита; акт опрессовки приложен (этап ВК).
		Сопротивление изоляции готовых линий; петля фаза-ноль для срабатывания автоматов	мегаомметр; прибор петли фаза-ноль	изоляция не менее 0,5 МОм; петля — по проекту	норматив (ПУЭ, гл. 1.8) / по проекту		
		Смесители, сифоны, гибкая подводка: пробный пуск воды	визуально под нагрузкой	нет подтёков в контрольное время	практика		
Р-16	Кухня и мебель Кухня и мебель: замер кухни снят по готовым стенам; чистовая электрика и сантехника подведены	Привязка выводов и розеток к модулям кухни; вытяжка, вентиляция	рулетка, сверка с листом кухни	по проекту кухни	практика		Акт передачи кухни; паспорта техники и гарантийные талоны.
		Тяга вентиляции у решёток	лист бумаги у решётки	бумага притягивается; при сомнениях — замер анемометром	практика		
Р-17	Сдача Финальная приёмка по таблицам СП 71: дефектная ведомость и акт	Стены, потолки, полы, плитка, двери, окна осмотр по чек-листу этапов выше	правило 2 м, уровень, щуп, боковой свет, влагомер	по таблицам выше	практика		Дефектная ведомость и акт приёмки; гарантия: по умолчанию претензии по качеству работ — 2 года, в договоре прописывается отдельно.
		Полный пакет документов: акты скрытых работ, протокол электролаборатории, акт опрессовки, исполнительные схемы, гарантийные обязательства	комплектность	пакет собран до подписи акта	практика		

Примечания

1. Метка основания: «норматив» — цифра подтверждена текстом СП, ГОСТ или ПУЭ; «практика» — отраслевая конвенция или один источник: к спору не годится без сверки первоисточника (СП 71.13330.2017, СП 29.13330, СП 163.1325800.2014, ПУЭ гл. 1.8, СП 73.13330, СП 30.13330).
2. Класс штукатурки (простая / улучшенная / высококачественная) и класс основания под окраску (Q3 или Q4) называются в договоре подряда: допуск выбирается по ним. Q-классы — не норматив, а согласованный сторонами критерий.
3. Акт скрытых работ подписывают до того, как работа закрыта следующим слоем (штукатуркой, плиткой, стяжкой, обшивкой): постфактум он слабее — осматривать нечего. Подписывают заказчик (или технадзор), подрядчик; при перепланировке — автор проекта. Каждую зону снимают до закрытия с рулеткой в кадре и привязкой к стене.
4. По умолчанию, если срок не прописан в договоре, претензии по качеству работ можно предъявить в течение 2 лет со дня приёмки; в договоре гарантийный срок и сроки на скрытые работы рекомендуется назвать явно.

	Лист	№ док.	Подпись	Дата	Проект: Квартира 56 м²			
Дизайнер	Кырлан А.С.			13.11.26	Чек-лист приёмки по этапам. Лист 3 из 3	Стадия	Лист	Листов
Проверил						П	С17	92
Н. контр.								
Утв.								

выпуск 13.11.2026 № 568a382a0d · стр. 91 из 92

Какому мастеру какие листы (номера — как в штампе)

Мастер	Что делает по альбому	Листы	Кроме чертежей — документы	Листов
Замерщик и прораб (до начала работ)	Контрольный обмер на голых стенах, сверка размеров и диагоналей, ответы на открытые вопросы до заказа	10, 12, 68–69	Задание на контрольный обмер; лист открытых вопросов	4
Гипсокартонщик и монтажник перегородок	Демонтаж и возведение перегородок, каркас, короба инсталляции, ниши, потолки; закладные под навесное	13–17, 36–39	Ведомость материалов каркаса; акт скрытых работ на каркас	9
Электрик	Группы щита, подрозетники и высоты, трассы, свет, управление светом, слаботочка, тёплый пол	40–47, 54–67	Таблица нагрузок; ведомость изделий; протокол электролаборатории	22
Сантехник	Выводы воды и канализации, разводка, аксонометрии, инсталляции, короба стояков	25–32, 54–67	Спецификация ВК; акт опрессовки; акт пролива	22
Монтажник вентиляции, отопления и кондиционеров	Вентиляция, радиаторы и тёплые полы, кондиционеры: места, размеры, трассы и дренаж	48–50	Акт опрессовки азотом (кондиционеры); фото воздуховодов до закрытия	3
Штукатур, шпаклёвщик, маляр, паркетчик	Основание стен, окраска и обои по колерной карте, полы и пороги, плинтус, узлы стыков	18–19, 51, 54–67, С1–С2, С12–С13	Колерная карта и выкрасы; спецификация отделочных материалов	21
Плиточник	Раскладка и подрезка плитки стен, пола и фартука, гидроизоляция, швы, выводы в плитке	30–31, 33, 52–67, С12–С13	Ведомость плитки; акт теста проливом	21
Монтажник дверей и окон	Заполнение проёмов: размеры коробок, открывание, пороги, скрытые двери	34–35	Ведомость проёмов; паспорта на полотна	2
Мебельщик, кухонный монтажник	Кухня и мебель на заказ: габариты, членение, фурнитура, связка с электрикой и сантехникой	16–17, 20–24, Д1–Д5	Ведомость изделий; замер кухни по готовым стенам	12
Заказчик и комплектатор	Что и когда покупать, сколько с запасом, во что это обойдётся; свет, декор и текстиль; визуализации как должно получиться	1–9, 11, 46, С3–С11, С14	Список покупок; смета; календарный график	21
Прораб и технадзор (приёмка)	Приёмка этапов, акты скрытых работ, дефектная ведомость	С14–С18	Чек-лист приёмки по этапам; календарный график	5

Примечания

1. Номера листов — как в основной надписи: основные подряд (1, 2, 3…), «Д» — детализация мебели, «С» — ведомости, спецификации, узлы и сметы, «П» — приложение единого комплекта. «12–18» — все листы с 12 по 18.
2. Лист может быть у нескольких мастеров: развёртка стены нужна электрику (высоты точек), сантехнику (выводы), отделочнику (материалы) и плиточнику (раскладка). Общие листы (обмер, список листов, перечень вопросов) прораб раздаёт всем.
3. Мастер работает по чертежам и берёт в руки то, что назначено ему здесь; закупки, смету и график ведёт заказчик с прорабом. Лист, которого нет в таблице ни у одного мастера, — вопрос прорабу: чей он.

	Лист	№ док.	Подпись	Дата	Проект: Квартира 56 м²			
Дизайнер	Кырлан А.С.			13.11.26	Лист → мастер	Стадия	Лист	Листов
Проверил						П	С18	92
Н. контр.								
Утв.								