ДИЗАЙН-ПРОЕКТ ИНТЕРЬЕРА

# Дом 331 м²

## *Шале*

**270,67 м²**

защищённый · тёплый · основательный · природный · камерный · после мороза — у огня

Современное шале 60 % + эко (eco-organic.json) 40 %: загородный дом у леса. Стены — шерстяной белый Joa's White No. 226 и молочный S 0804-Y30R, потолки — известковый Slaked Lime No. 105; второй план — выцветший оливковый V451, шалфей S 3020-G30Y, песчаник X463; акценты — хвойный S 7020-G10Y, терракота Red Earth No. 64, брусника Eating Room Red No. 43. Дерево — дуб и лиственница под маслом, камень у камина.

ПАЛИТРА 60 / 30 / 10

| F&B No. 226 | NCS S 0804-Y30R | Little Greene No. 105 | V451 | NCS S 3020-G30Y |
|---|---|---|---|---|
| 60 % | 60 % | 60 % | 30 % | 30 % |


АВТОР ПРОЕКТА

Кырлан Александр Сергеевич


Октябрь 2026

Визуализация 1 · Вид сверху (3D): планировка с мебелью, текстилем и декором

| ОБЪЕКТ | ОБЩАЯ ПЛОЩАДЬ | ПОМЕЩЕНИЙ |
|---|---|---|
| Дом 331 м² | 270,67 м² | 20, из них жилых 6 |
| **СТИЛЬ** | **СТАДИЯ** | **ШИФР** |
| Шале | Рабочий проект | ГД-2026-010-АИ |

КАК ОСТАВИТЬ ПРАВКУ

Нажмите кнопку «Правка к этому листу» в правом верхнем углу любого листа — лист откроется на сайте студии: отметьте место на чертеже и наговорите замечание голосом или напишите текстом.

Или откройте все листы проекта:

alex1986-rgb.github.io/linea-design-studio/review.html?p=gost-dom331

| | | | | | Проект: Дом 331 м² | | | |
|---|---|---|---|---|---|---|---|---|
| | Лист | № док. | Подпись | Дата | Титульный лист | Стадия | Лист | Листов |
| Дизайнер | Кырлан А.С. | | | 19.10.26 | | П | 1 | 156 |


выпуск 18.10.2026 № 8cd922c868 · стр. 1 из 156

Правка к этому листу

## Список листов

| Лист | Наименование |
|---|---|
| 1 | Титульный лист |
| 2 | Список листов |
| 3 | План планировки от заказчика · 1-й этаж |
| 4 | План планировки от заказчика · Мансарда |
| 5 | План монтажный · 1-й этаж |
| 6 | План монтажный · Мансарда |
| 7 | Кухня (пом. 1). Монтажная схема |
| 8 | Шкафы. Монтажная схема. Лист 1 из 2 |
| 9 | Шкафы. Монтажная схема. Лист 2 из 2 |
| 10 | Карта покрытий стен · 1-й этаж |
| 11 | Карта покрытий стен · Мансарда |
| 12 | Колерная карта |
| 13 | План размещения мебели и оборудования · 1-й этаж |
| 14 | План размещения мебели и оборудования · Мансарда |
| 15 | Спецификация мебели и оборудования |
| 16 | Спецификация мебели и оборудования (продолжение) |
| 17 | Спецификация мебели и оборудования (продолжение) |
| 18 | Спецификация мебели и оборудования (продолжение) |
| 19 | Ведомости изделий, техники и фурнитуры |
| 20 | План выводов сантехники · 1-й этаж |
| 21 | План выводов сантехники · Мансарда |
| 22 | Схема разводки водопровода и канализации · 1-й этаж |
| 23 | Схема разводки водопровода и канализации · Мансарда |
| 24 | Спецификация сантехнического оборудования |
| 25 | Раскладка плитки. Санузел 1 этажа. Развёртки стен |
| 26 | Раскладка плитки. Санузел мастер. Развёртки стен |
| 27 | Раскладка плитки. Санузел 2. Развёртки стен |
| 28 | План размещения дверей · 1-й этаж |
| 29 | План размещения дверей · Мансарда |
| 30 | Лестница Л-1 |
| 31 | План потолков · 1-й этаж |
| 32 | План потолков · Мансарда |
| 33 | Разрезы и узлы потолков |
| 34 | План розеток и электровыводов · 1-й этаж |
| 35 | План розеток и электровыводов · Мансарда |
| 36 | План слаботочных сетей · 1-й этаж |
| 37 | План слаботочных сетей · Мансарда |
| 38 | План освещения · 1-й этаж |
| 39 | План освещения · Мансарда |
| 40 | Спецификация светильников и сценарии освещения |

| Лист | Наименование |
|---|---|
| 41 | Управление светильниками · 1-й этаж |
| 42 | Управление светильниками · Мансарда |
| 43 | План вентиляции · 1-й этаж |
| 44 | План вентиляции · Мансарда |
| 45 | План отопления · 1-й этаж |
| 46 | План отопления · Мансарда |
| 47 | План покрытий пола · 1-й этаж |
| 48 | План покрытий пола · Мансарда |
| 49 | Раскладка плитки. Планы полов |
| 50 | Раскладка плитки. Котельная. Прихожая. Тамбур. Веранда |
| 51 | Визуализация. Вид сверху |
| 52 | Визуализация. Вид сверху |
| 53 | Визуализация: Кухня-столовая |
| 54 | Визуализация: Кухня-столовая |
| 55 | Развёртка стены А. Кухня-столовая (пом. 1), кухонный фронт |
| 56 | Развёртка стены Б. Кухня-столовая (пом. 1) |
| 57 | Развёртка стены В. Кухня-столовая (пом. 1) |
| 58 | Развёртка стены Г. Кухня-столовая (пом. 1) |
| 59 | Визуализация: Кабинет-гостевая |
| 60 | Визуализация: Кабинет-гостевая |
| 61 | Развёртка стены А. Кабинет-гостевая (пом. 2) |
| 62 | Развёртка стены Б. Кабинет-гостевая (пом. 2) |
| 63 | Развёртка стены В. Кабинет-гостевая (пом. 2) |
| 64 | Развёртка стены Г. Кабинет-гостевая (пом. 2) |
| 65 | Визуализация: Санузел 1 этажа |
| 66 | Развёртка стены А. Санузел 1 этажа (пом. 3) |
| 67 | Развёртки стен Б, В. Санузел 1 этажа (пом. 3) |
| 68 | Развёртка стены Г. Санузел 1 этажа (пом. 3) |
| 69 | Визуализация: Котельная |
| 70 | Развёртка стены А. Котельная (пом. 4) |
| 71 | Развёртки стен Б, Г. Котельная (пом. 4) |
| 72 | Визуализация гостиной |
| 73 | Визуализация гостиной |
| 74 | Визуализация гостиной |
| 75 | Развёртка стены А. Гостиная (пом. 5) |
| 76 | Развёртка стены Б. Гостиная (пом. 5) |
| 77 | Развёртка стены В. Гостиная (пом. 5) |
| 78 | Развёртка стены Г. Гостиная (пом. 5) |
| 79 | Визуализация: Холл с лестницей |
| 80 | Развёртка стены А. Холл с лестницей (пом. 6) |

| Лист | Наименование |
|---|---|
| 81 | Развёртка стены В. Холл с лестницей (пом. 6) |
| 82 | Визуализация кладовой |
| 83 | Развёртки стен. Кладовая (пом. 7) |
| 84 | Визуализация прихожей |
| 85 | Визуализация прихожей |
| 86 | Развёртка стены А. Прихожая (пом. 8) |
| 87 | Развёртка стены Б. Прихожая (пом. 8) |
| 88 | Развёртка стены В. Прихожая (пом. 8) |
| 89 | Развёртка стены Г. Прихожая (пом. 8) |
| 90 | Развёртки стен. Тамбур (пом. 9) |
| 91 | Визуализация: Гараж |
| 92 | Развёртка стены А. Гараж (пом. 10) |
| 93 | Развёртка стены Б. Гараж (пом. 10) |
| 94 | Развёртка стены В. Гараж (пом. 10) |
| 95 | Развёртка стены Г. Гараж (пом. 10) |
| 96 | Визуализация: Веранда |
| 97 | Развёртка стены А. Веранда (пом. 11) |
| 98 | Развёртка стены В. Веранда (пом. 11) |
| 99 | Развёртка стены Г. Веранда (пом. 11) |
| 100 | Визуализация: Крыльцо |
| 101 | Развёртки стен. Крыльцо (пом. 12) |
| 102 | Визуализация: Спальня мастер |
| 103 | Визуализация: Спальня мастер |
| 104 | Развёртка стены А. Спальня мастер (пом. 13) |
| 105 | Развёртка стены Б. Спальня мастер (пом. 13) |
| 106 | Развёртка стены В. Спальня мастер (пом. 13) |
| 107 | Развёртка стены Г. Спальня мастер (пом. 13) |
| 108 | Визуализация: Гардеробная мастер |
| 109 | Развёртки стен А, Б. Гардеробная мастер (пом. 14) |
| 110 | Развёртки стен В, Г. Гардеробная мастер (пом. 14) |
| 111 | Визуализация: Санузел мастер |
| 112 | Развёртка стены А. Санузел мастер (пом. 15) |
| 113 | Развёртка стены Б. Санузел мастер (пом. 15) |
| 114 | Развёртка стены В. Санузел мастер (пом. 15) |
| 115 | Развёртка стены Г. Санузел мастер (пом. 15) |
| 116 | Визуализация: Спальня 2 |

| | | | | |
|---|---|---|---|---|
| | Лист | № док. | Подпись | Дата |
| Дизайнер | Кырлан А.О. | | | 19.10.26 |

Проект: Дом 331 м²

Список листов

| Стадия | Лист | Листов |
|---|---|---|
| П | 2 | 156 |

выпуск 18.10.2026 № 8cd922c868 · стр. 2 из 156

Правка к этому листу

## Отметки по высоте

| | |
|---|---|
| **±0,000** | чистый пол пом. 1, 2, 4–10; отсчёт высот |
| **−0,015** | чистый пол пом. 3, ниже на 15 мм |
| **−0,030** | чистый пол пом. 11, 12, ниже на 30 мм |
| **плита** | верх плиты разный: −0,064, −0,170 (задание на обмер) |
| **сущ. пол** | снимается до плиты; не замерен (задание на обмер) |

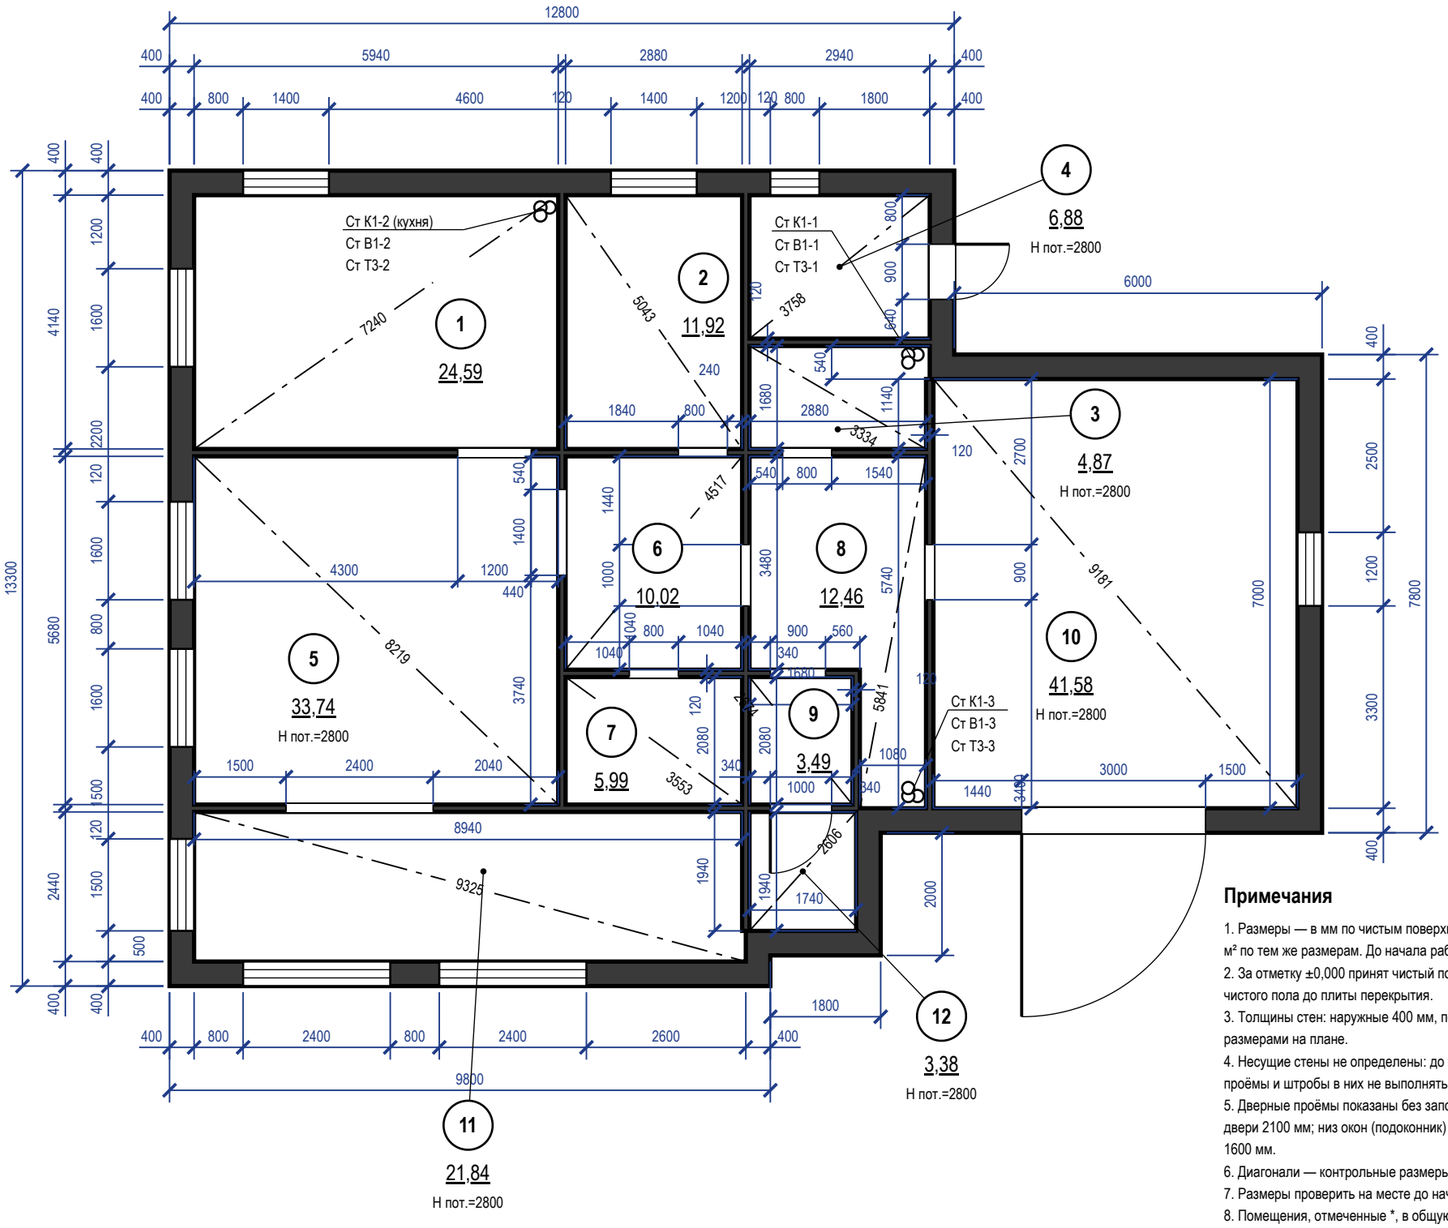


## Экспликация помещений

| № | Наименование | Площадь, м² |
|---|---|---|
| 1 | Кухня-столовая | 24,59 |
| 2 | Кабинет-гостевая | 11,92 |
| 3 | Санузел 1 этажа | 4,87 |
| 4 | Котельная | 6,88 |
| 5 | Гостиная | 33,74 |
| 6 | Холл с лестницей | 10,02 |
| 7 | Кладовая | 5,99 |
| 8 | Прихожая | 12,46 |
| 9 | Тамбур | 3,49 |
| 10 | Гараж | 41,58 |
| 11 | Веранда * | 21,84 |
| 12 | Крыльцо * | 3,38 |
| | **Итого (общая площадь)** | **270,67** |

## Условные обозначения

- существующие стены (сечение)
- окно (рама, остекление)
- проём существующий, без заполнения (откосы)
- стояк: К1 — канализация, В1 — ХВС, Т3 — ГВС
- диагональ помещения — контроль прямоугольности
- (1) номер помещения, площадь м²

## Примечания

1. Размеры — в мм по чистым поверхностям стен до отделки (по плану заказчика); площади — в м² по тем же размерам. До начала работ выполнить контрольный обмер.
2. За отметку ±0,000 принят чистый пол, не существующий (блок отметок). Н пот. — высота от чистого пола до плиты перекрытия.
3. Толщины стен: наружные 400 мм, перегородки 120 мм; отличающиеся толщины и уступы размерами на плане.
4. Несущие стены не определены: до технического заключения все стены считать несущими; проёмы и штробы в них не выполнять.
5. Дверные проёмы показаны без заполнения; высота дверных проёмов 2100, 2300 мм, проёмов без двери 2100 мм; низ окон (подоконник) 900, 1200 мм от чистого пола, высота окон 1500, 900, 1600 мм.
6. Диагонали — контрольные размеры; расхождение более 5 мм подписать на плане как перекос.
7. Размеры проверить на месте до начала работ; расхождение контрольных промеров ≤ 2 %.
8. Помещения, отмеченные *, в общую площадь квартиры не входят.

| | | | | | |
|---|---|---|---|---|---|
| | | | | | Проект: Дом 331 м² |
| | Лист | № док. | Подпись | Дата | План планировки от заказчика · 1-й этаж |
| Дизайнер | Кырлан А.С. | | | 19.10.26 | |

| Стадия | Лист | Листов |
|---|---|---|
| П | 3 | 156 |

выпуск 18.10.2026 № 8cd922c868 · стр. 3 из 156

Правка к этому листу

## Отметки по высоте

**±0,000** чистый пол пом. 13, 14, 16–19; отсчёт высот
**−0,015** чистый пол пом. 15, 20, ниже на 15 мм
**−0,064** верх плиты — расчёт, не замер (задание на обмер)
**сущ. пол** снимается до плиты; не замерен (задание на обмер)

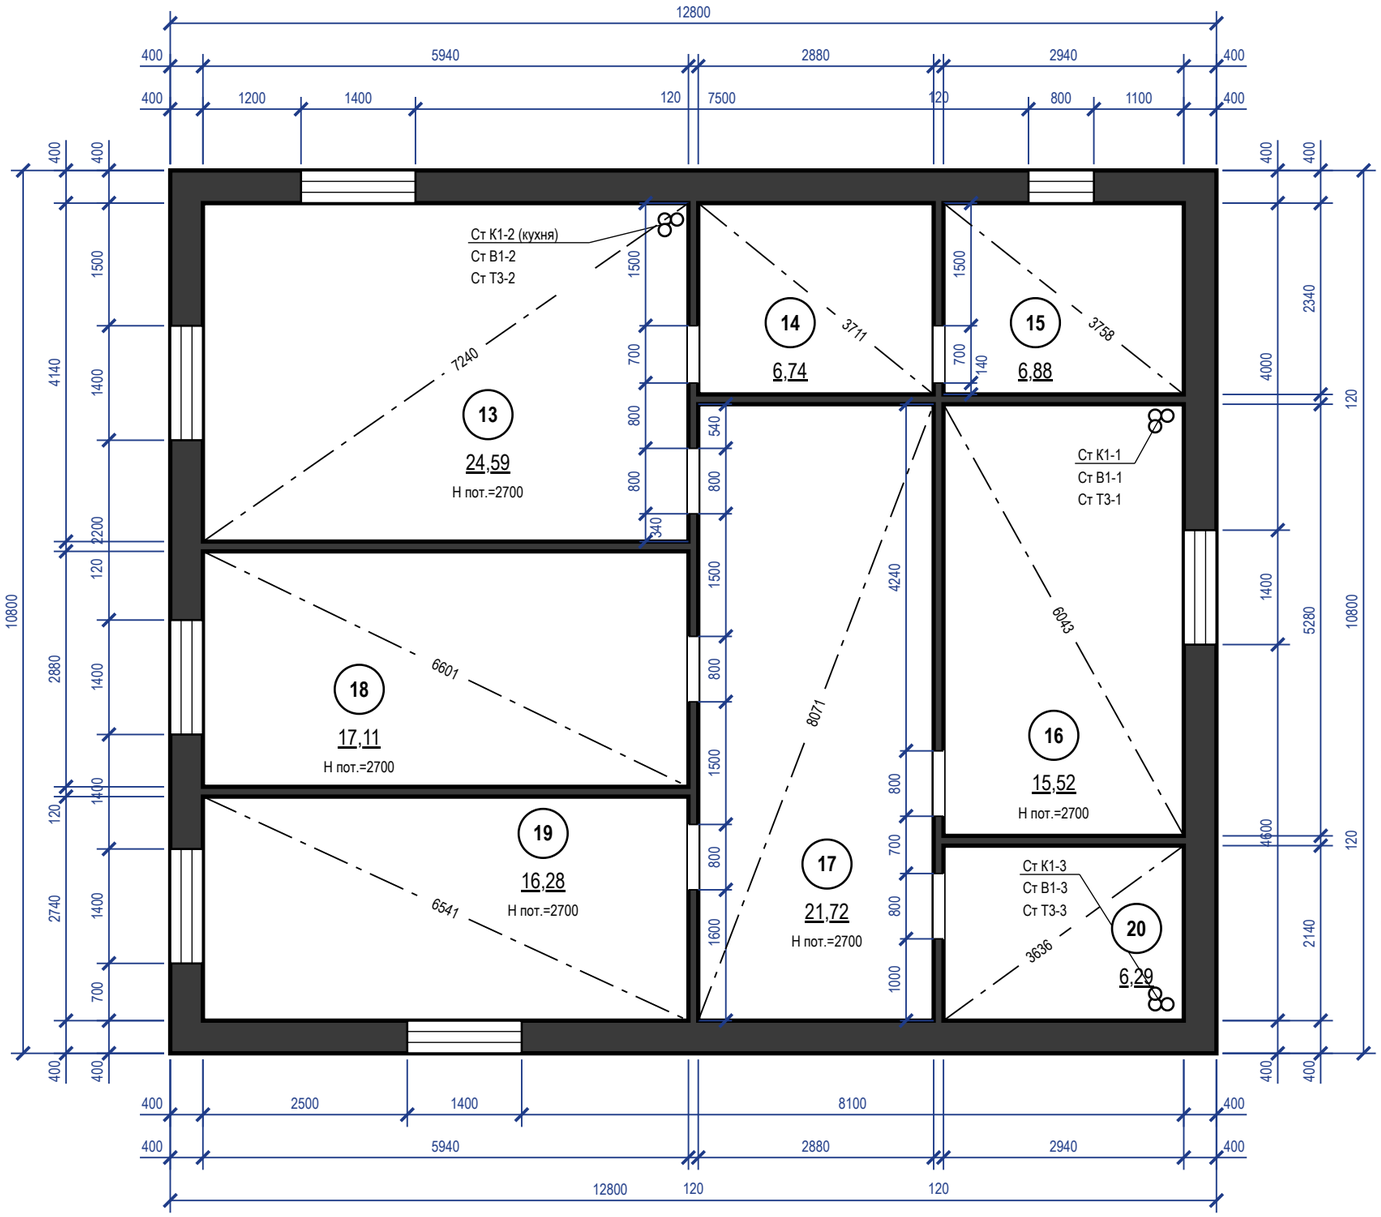


## Экспликация помещений

| № | Наименование | Площадь, м² |
|---|---|---|
| 13 | Спальня мастер | 24,59 |
| 14 | Гардеробная мастер | 6,74 |
| 15 | Санузел мастер | 6,88 |
| 16 | Спальня 2 | 15,52 |
| 17 | Холл мансарды | 21,72 |
| 18 | Спальня 3 | 17,11 |
| 19 | Спальня 4 | 16,28 |
| 20 | Санузел 2 | 6,29 |
| | **Итого (общая площадь)** | **270,67** |

## Условные обозначения

- существующие стены (сечение)
- окно (рама, остекление)
- проём существующий, без заполнения (откосы)
- стояк: К1 — канализация, В1 — ХВС, Т3 — ГВС
- диагональ помещения — контроль прямоугольности
- (1) номер помещения, площадь м²

## Примечания

1. Размеры — в мм по чистым поверхностям стен до отделки (по плану заказчика); площади — в м² по тем же размерам. До начала работ выполнить контрольный обмер.
2. За отметку ±0,000 принят чистый пол, не существующий (блок отметок). Н пот. — высота от чистого пола до плиты перекрытия.
3. Толщины стен: наружные 400 мм, перегородки 120 мм; отличающиеся толщины и уступы размерами на плане.
4. Несущие стены не определены: до технического заключения все стены считать несущими; проёмы и штробы в них не выполнять.
5. Дверные проёмы показаны без заполнения; высота дверных проёмов 2100 мм; низ окон (подоконник) 900, 1500 мм от чистого пола, высота окон 1500, 800 мм.
6. Диагонали — контрольные размеры; расхождение более 5 мм подписать на плане как перекос.
7. Размеры проверить на месте до начала работ; расхождение контрольных промеров ≤ 2 %.

| | | | | | |
|---|---|---|---|---|---|
| | | | | | Проект: Дом 331 м² |
| | Лист | № док. | Подпись | Дата | План планировки от заказчика · Мансарда |
| Дизайнер | Кырлан А.С. | | | 19.10.26 | |

| Стадия | Лист | Листов |
|---|---|---|
| П | 4 | 156 |

выпуск 18.10.2026 № 8cd922c868 · стр. 4 из 156

Правка к этому листу

## Экспликация помещений

| № | Наименование | Площадь, м² |
|---|---|---|
| 1 | Кухня-столовая | 24,59 |
| 2 | Кабинет-гостевая | 11,92 |
| 3 | Санузел 1 этажа | 4,87 |
| 4 | Котельная | 6,88 |
| 5 | Гостиная | 33,74 |
| 6 | Холл с лестницей | 10,02 |
| 7 | Кладовая | 5,99 |
| 8 | Прихожая | 12,46 |
| 9 | Тамбур | 3,49 |
| 10 | Гараж | 41,58 |
| 11 | Веранда * | 21,84 |
| 12 | Крыльцо * | 3,38 |
| | **Итого (общая площадь)** | **270,67** |

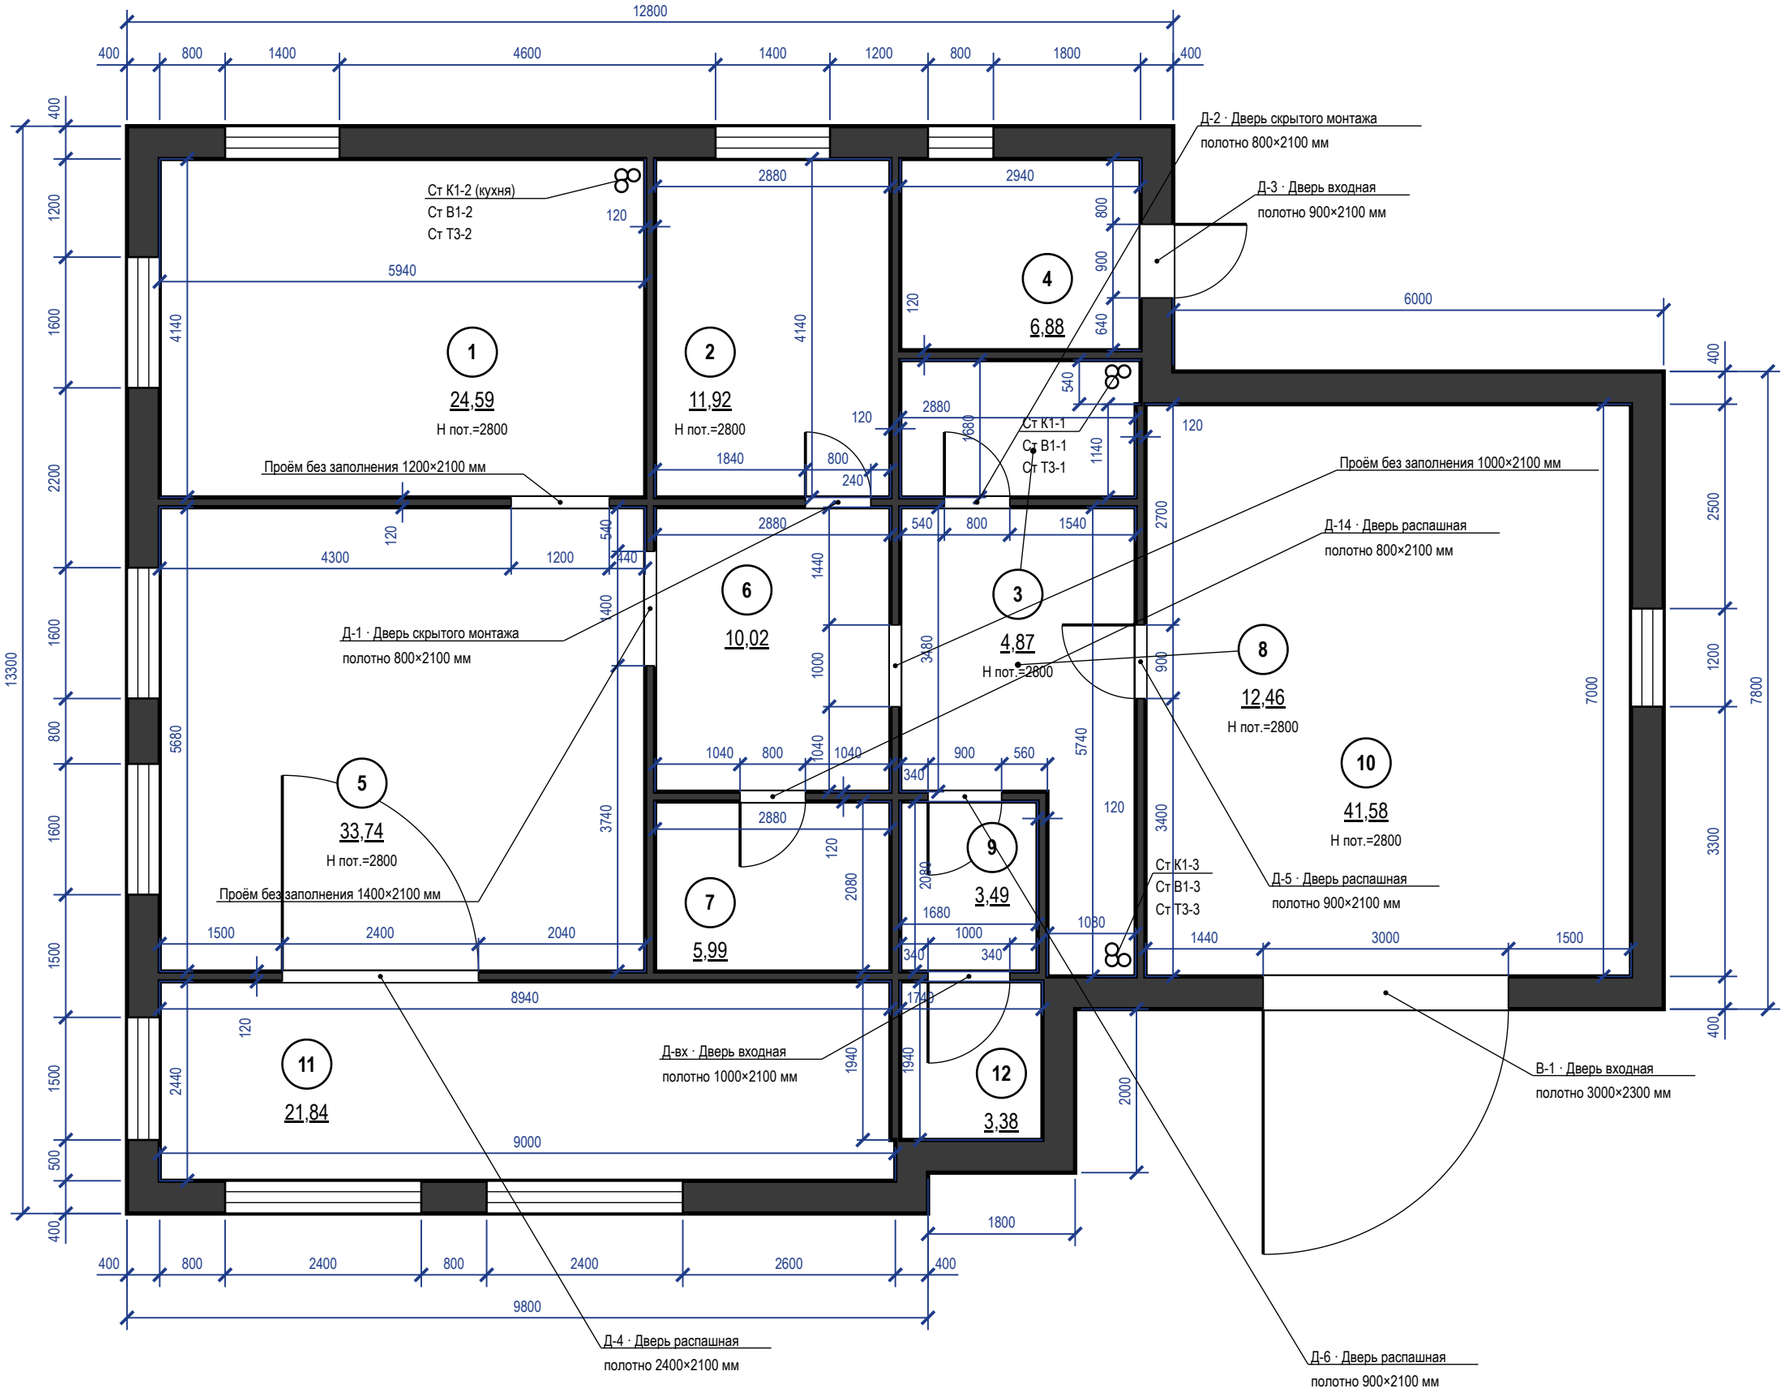


## Примечания

1. Размеры — в мм от чистовых поверхностей стен до отделки; размеры уточнить по месту до начала работ.
2. Новые перегородки и облицовки — синим; каркас и обшивка — по выноскам.
3. Несущие стены не изменять: проёмы, ниши и штробы в них — только по техническому заключению.

| | | | | | |
|---|---|---|---|---|---|
| | | | | | Проект: Дом 331 м² |
| | Лист | № док. | Подпись | Дата | План монтажный · 1-й этаж |
| Дизайнер | Кырлан А.С. | | | 19.10.26 | Стадия: П; Лист: 5; Листов: 156 |

выпуск 18.10.2026 № 8cd922c868 · стр. 5 из 156

Правка к этому листу

## Экспликация помещений

| № | Наименование | Площадь, м² |
|---|---|---|
| 13 | Спальня мастер | 24,59 |
| 14 | Гардеробная мастер | 6,74 |
| 15 | Санузел мастер | 6,88 |
| 16 | Спальня 2 | 15,52 |
| 17 | Холл мансарды | 21,72 |
| 18 | Спальня 3 | 17,11 |
| 19 | Спальня 4 | 16,28 |
| 20 | Санузел 2 | 6,29 |
| | **Итого (общая площадь)** | **270,67** |

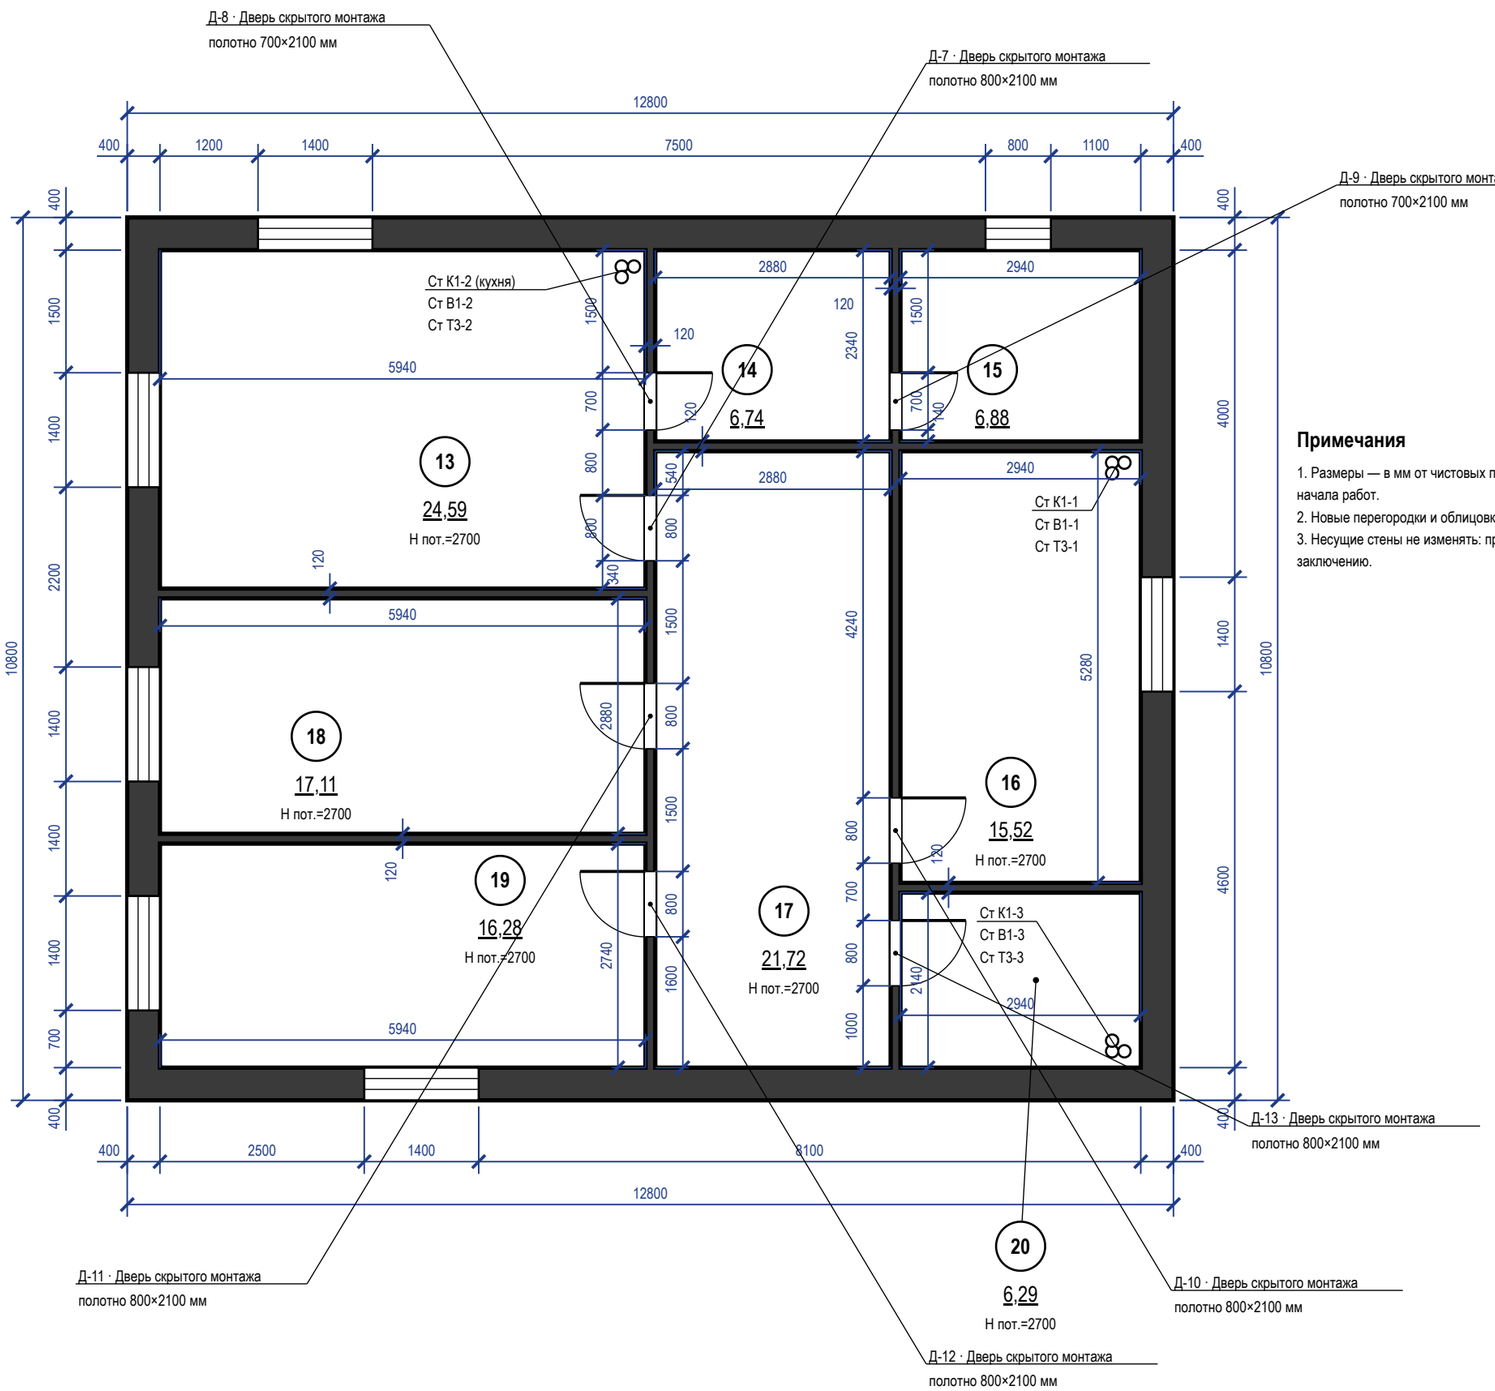


## Примечания

1. Размеры — в мм от чистовых поверхностей стен до отделки; размеры уточнить по месту до начала работ.
2. Новые перегородки и облицовки — синим; каркас и обшивка — по выноскам.
3. Несущие стены не изменять: проёмы, ниши и штробы в них — только по техническому заключению.

| | | | | | |
|---|---|---|---|---|---|
| | Лист | № док. | Подпись | Дата | |
| Дизайнер | Кырлан А.С. | | | 19.10.26 | |

Проект: Дом 331 м²

План монтажный · Мансарда

| Стадия | Лист | Листов |
|---|---|---|
| П | 6 | 156 |

выпуск 18.10.2026 № 8cd922c868 · стр. 6 из 156

Правка к этому листу

## Привязка выводов и крепление модулей

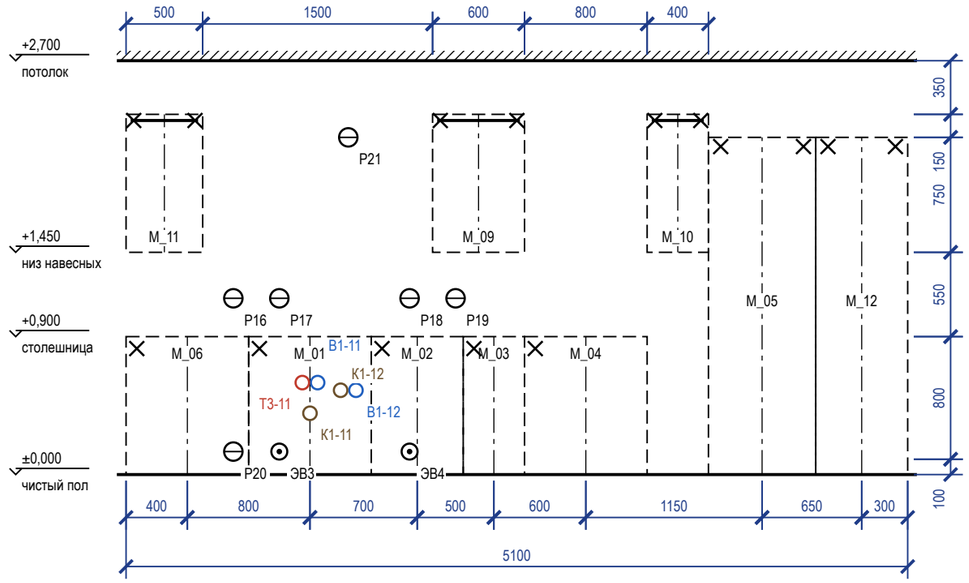


## План столешницы

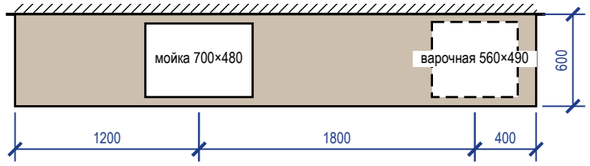


### Примечания

1. Выводы — по проекту электрики и ВК; привязка по горизонтали — от оси модуля (плюс — вправо по виду), по высоте — от чистого пола до оси вывода.
2. Пенал — уголки к стене 2 шт. сверху; нижние модули — стяжками между собой и уголком к стене; ряд выставить по уровню опорами цоколя.
3. Розетки над столешницей — не ниже 150 мм над ней и не за корпусом техники; розетка за ПММ, духовым шкафом и холодильником — только в соседнем модуле или в зоне цоколя с доступом.
4. Столешница — вырезы по шаблонам выбранных моделей мойки и варочной панели; торцы у стены — герметик, пристеночный плинтус.

### Привязка выводов к осям модулей

| Код | Назначение | Модуль | От оси, мм | H, мм | Размещение |
|---|---|---|---|---|---|
| P16 | розетка ×2 — фартук: мелкая техника | M_06 | +300 | 1150 | над столешницей (фартук) |
| P20 | розетка — холодильник встроенный M20 (розетка в модуле M21) | M_06 | +300 | 150 | в соседнем модуле, за ящиком |
| P17 | розетка ×2 — фартук: мелкая техника | M_01 | −200 | 1150 | над столешницей (фартук) |
| ЭВ3 | вывод кабеля — варочная панель M22 | M_01 | −200 | 150 | в модуле мойки |
| T3-11 | T3 — межос. 100 | M_01 | −50 | 600 | в модуле мойки |
| K1-11 | K1 Ø50 — мойка | M_01 | 0 | 400 | в модуле мойки |
| B1-11 | B1 — межос. 100 | M_01 | +50 | 600 | в модуле мойки |
| K1-12 | K1 Ø40 — слив ПММ в шкафу мойки | M_01 | +200 | 550 | в модуле мойки |
| P21 | розетка — вытяжка M25 (в модуле, съёмная панель) | M_01 | +250 | 2200 | над столешницей (фартук) |
| B1-12 | B1 — кран ПММ в шкафу мойки | M_01 | +300 | 550 | в модуле мойки |
| P18 | розетка ×2 — фартук: мелкая техника | M_02 | −50 | 1150 | над столешницей (фартук) |
| ЭВ4 | вывод кабеля — духовой шкаф M22 (вывод в соседнем модуле M23) | M_02 | −50 | 150 | за ПММ — перенести в соседний модуль |
| P19 | розетка ×2 — фартук: мелкая техника | M_02 | +250 | 1150 | над столешницей (фартук) |

### Зазоры под отделку

| Поверхность | Отделка | Зазор, мм | Учесть |
|---|---|---|---|
| фартук | керамогранит | 10 | от чернового основания до корпуса навесных и столешницы |
| стены | окраска | 5 | под штукатурку и шпаклёвку за пеналом |
| пол | инженерная доска | | цоколь — после укладки пола, опоры ±20 мм |

### Условные обозначения

- навесной модуль (невидимый контур)
- ось модуля (от неё — привязка вывода)
- анкер / уголок крепления к стене
- розетка на стене
- вывод кабеля к технике
- B1 — вывод воды B1 / T3, канализации K1

| | Лист | № док. | Подпись | Дата |
|---|---|---|---|---|
| Дизайнер | Кырлан А.С. | | | 19.10.26 |

Проект: Дом 331 м²

Кухня (пом. 1). Монтажная схема

| Стадия | Лист | Листов |
|---|---|---|
| П | 7 | 156 |

Правка к этому листу

### Система хранения M_17 (пом. 4)

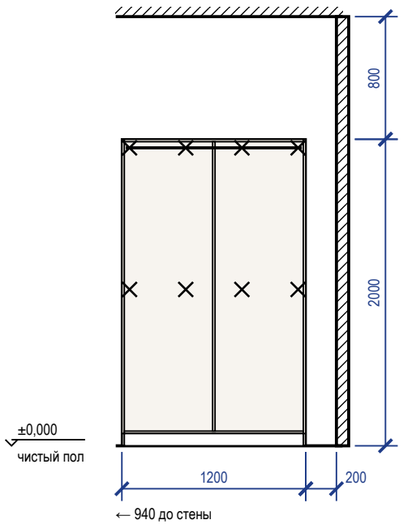


### Система хранения M_23 (пом. 7)

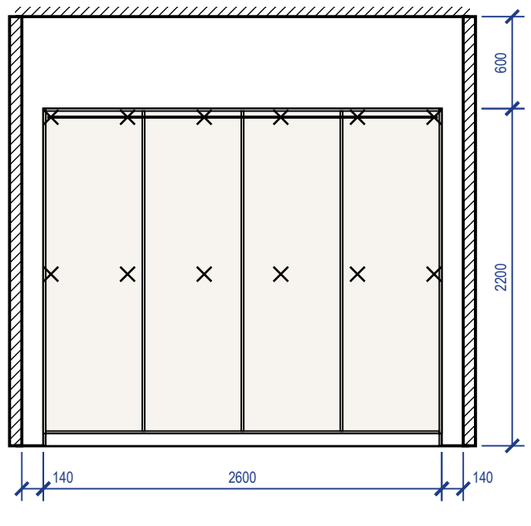


### Шкаф-купе M_24 (пом. 8)

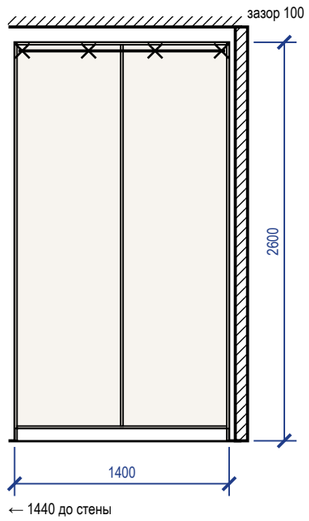


### Система хранения M_26 (пом. 10)

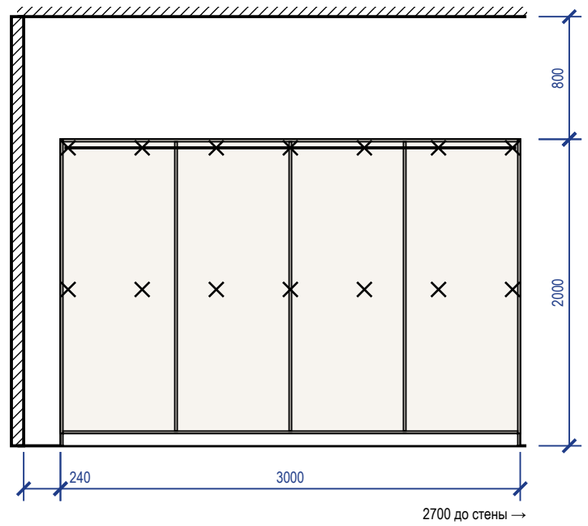


## Крепление и зазоры под отделку (изделия листа 1)

| Марка | Помещение, стена | Основание | Отделка стены | Зазор, мм | Крепёж по планке | От опрокидывания |
|---|---|---|---|---|---|---|
| M_17 | Котельная (4), стена Г | по основанию — см. таблицу крепежа | окраска | 5 | анкер 8 шт. (2 ряда) | уголки 2 шт. |
| M_23 | Кладовая (7), стена В | по основанию — см. таблицу крепежа | окраска | 5 | анкер 12 шт. (2 ряда) | уголки 2 шт. |
| M_24 | Прихожая (8), стена А | по основанию — см. таблицу крепежа | окраска | 5 | анкер 4 шт., шаг 433 | уголки 2 шт. |
| M_26 | Гараж (10), стена А | по основанию — см. таблицу крепежа | окраска | 5 | анкер 14 шт. (2 ряда) | true |

## Крепёж по основанию стены

| Основание стены | Крепёж |
|---|---|
| бетон, ж/б | анкер-шуруп 7,5×72 или дюбель 8×60 с шурупом 5×70 |
| кирпич полнотелый | дюбель 8×80 с шурупом 5×90 |
| газобетон, пазогребень | дюбель для газобетона 10×100 или химический анкер |
| гипсокартон | закладная до обшивки (брус 40×80 или фанера 18 мм), саморез в закладную |

## Условные обозначения

- анкер / уголок крепления к стене
- корпус и полки ЛДСП (вид на стену)
- компенсатор — короб до потолка

## Примечания

1. Установочные размеры — от чистого пола и чистых стен; перед установкой контрольный замер после отделки.
2. Порядок: корпус выставить по уровню опорами цоколя → закрепить к стене по задней планке → навесить двери и фасады, отрегулировать зазоры → подогнать и закрепить компенсатор.
3. Анкеры — с шагом не более 500 мм, не ближе 50 мм от края планки; на ГКЛ только в закладную, установленную до обшивки.
4. Скрытые коммуникации под анкеры проверить детектором; трассы электрики по плану розеток.
5. Монтажная схема на 2 листах, лист 1 из 2; продолжение — на следующем листе схемы. Условные обозначения, таблица крепежа по основанию и примечания повторены на каждом листе.

| | | | | | | |
|---|---|---|---|---|---|---|
| | | | | | Проект: Дом 331 м² | |
| | Лист | № док. | Подпись | Дата | Шкафы. Монтажная схема. Лист 1 из 2 | Стадия / Лист / Листов |
| Дизайнер | Кырлан А.С. | | | 19.10.26 | | П / 8 / 156 |

выпуск 18.10.2026 № 8cd922c868 · стр. 8 из 156

Правка к этому листу

**Система хранения M_43 пом. 14**

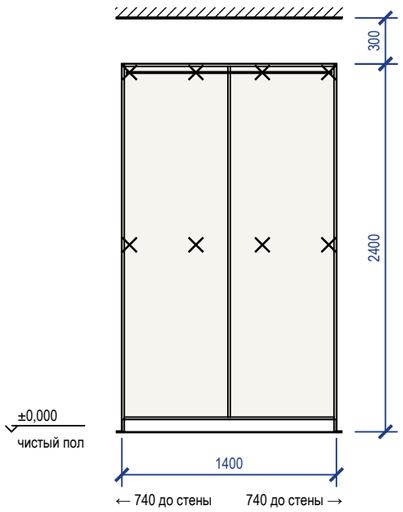


**Шкаф распашной M_46 (пом. 16)**

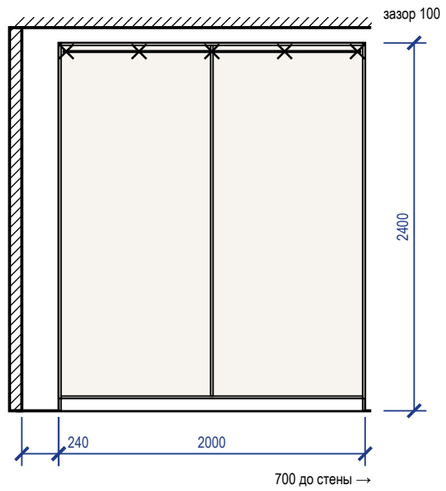


**Система хранения M_49 (пом. 17)**

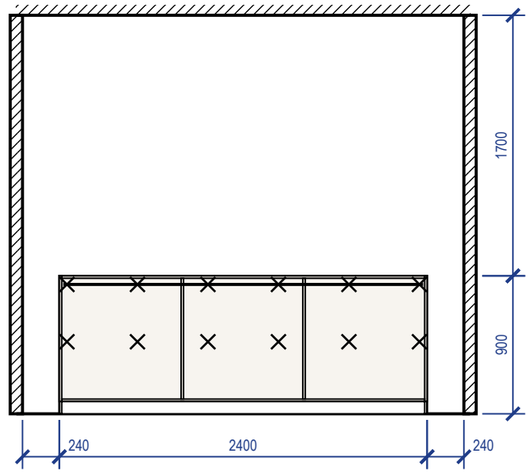


**Шкаф распашной M_53 (пом. 18)**

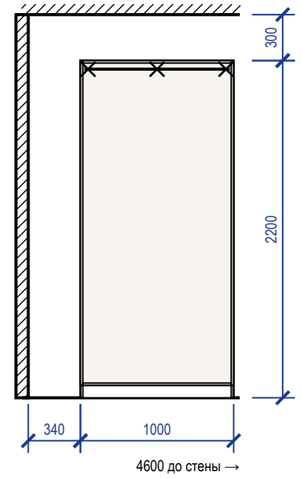


**Шкаф распашной M_56 пом. 19**

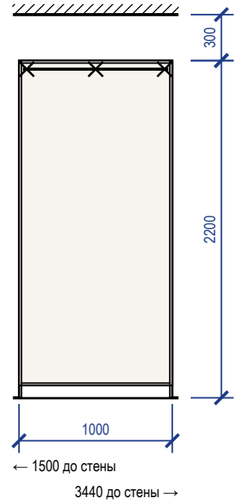


## Крепление и зазоры под отделку (изделия листа 2)

| Марка | Помещение, стена | Основание | Отделка стены | Зазор, мм | Крепёж по планке | От опрокидывания |
|---|---|---|---|---|---|---|
| M_43 | Гардеробная мастер (14), стена B | по основанию — см. таблицу крепежа | окраска | 5 | анкер 8 шт. (2 ряда) | уголки 2 шт. |
| M_46 | Спальня 2 (16), стена A | по основанию — см. таблицу крепежа | окраска | 5 | анкер 5 шт., шаг 475 | уголки 2 шт. |
| M_49 | Холл мансарды (17), стена B | по основанию — см. таблицу крепежа | окраска | 5 | анкер 12 шт. (2 ряда) | true |
| M_53 | Спальня 3 (18), стена B | по основанию — см. таблицу крепежа | окраска | 5 | анкер 3 шт., шаг 450 | уголки 2 шт. |
| M_56 | Спальня 4 (19), стена A | по основанию — см. таблицу крепежа | окраска | 5 | анкер 3 шт., шаг 450 | уголки 2 шт. |

## Крепёж по основанию стены

| Основание стены | Крепёж |
|---|---|
| бетон, ж/б | анкер-шуруп 7,5×72 или дюбель 8×60 с шурупом 5×70 |
| кирпич полнотелый | дюбель 8×80 с шурупом 5×90 |
| газобетон, пазогребень | дюбель для газобетона 10×100 или химический анкер |
| гипсокартон | закладная до обшивки (брус 40×80 или фанера 18 мм), саморез в закладную |

## Условные обозначения

- × — анкер / уголок крепления к стене
- ▭ — корпус и полки ЛДСП (вид на стену)
- ▨ — компенсатор — короб до потолка

## Примечания

1. Установочные размеры — от чистого пола и чистых стен; перед установкой контрольный замер после отделки.
2. Порядок: корпус выставить по уровню опорами цоколя → закрепить к стене по задней планке → навесить двери и фасады, отрегулировать зазоры → подогнать и закрепить компенсатор.
3. Анкеры — с шагом не более 500 мм, не ближе 50 мм от края планки; на ГКЛ только в закладную, установленную до обшивки.
4. Скрытые коммуникации под анкеры проверить детектором; трассы электрики по плану розеток.
5. Монтажная схема на 2 листах, лист 2 из 2. Условные обозначения, таблица крепежа по основанию и примечания повторены на каждом листе.

| | | | | | | |
|---|---|---|---|---|---|---|
| | | | | | Проект: Дом 331 м² | |
| | Лист | № док. | Подпись | Дата | Шкафы. Монтажная схема. Лист 2 из 2 | Стадия / Лист / Листов |
| Дизайнер | Кырлан А.С. | | | 19.10.26 | | П / 9 / 156 |

выпуск 18.10.2026 № 8cd922c868 · стр. 9 из 156

Правка к этому листу

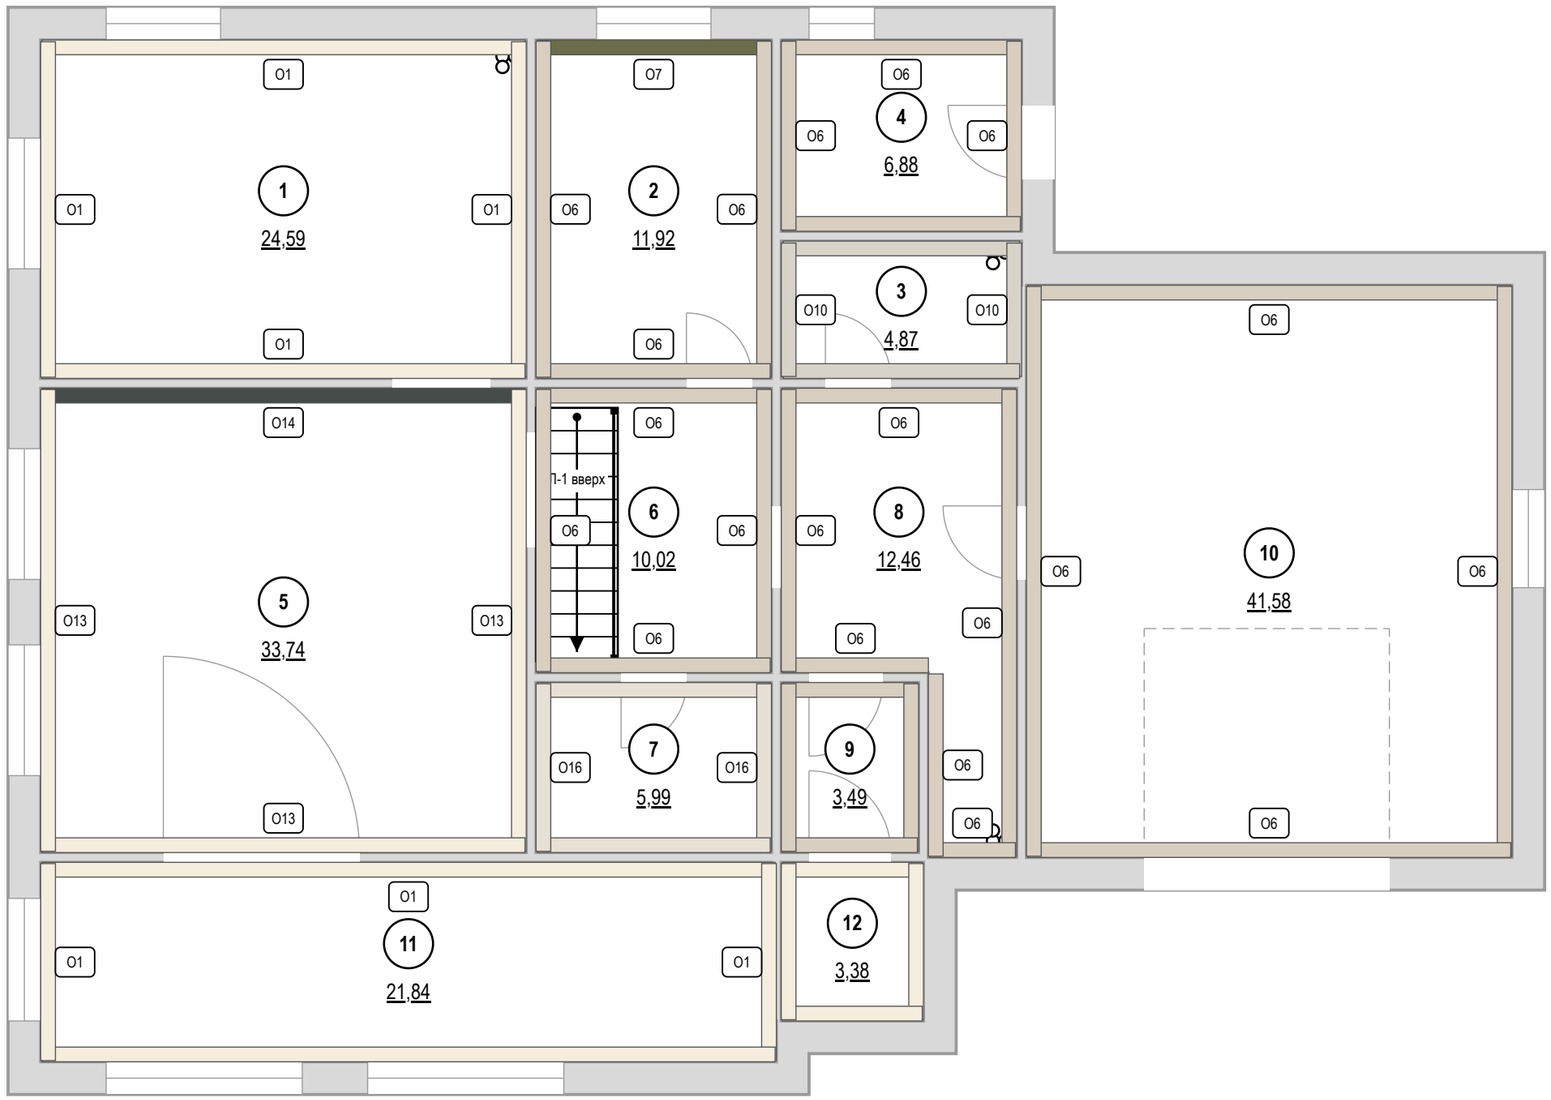


## Покрытия стен

| Марка | Покрытие | Помещение: S, м² | Итого, м² |
|---|---|---|---|
| О1 | окраска Tikkurila · S 0804-Y30R «S 0804-Y30R» | 1: 45,0; 11: 49,3; 12: 18,4 | 112,7 |
| О6 | окраска Farrow & Ball · No. 226 «Joa's White» | 2: 27,7; 4: 26,6; 6: 25,6; 8: 38,5; 9: 16,7; 10: 62,3 | 197,4 |
| О7 | окраска Farrow & Ball · No. 298 «Bancha» | 2: 5,5 | 5,5 |
| О10 | облицовка плиткой Atlas Concorde · A8UZ «Marvel Travertine» 600×1200 мм | 3: 20,1 | 20,1 |
| О13 | окраска Tikkurila · S 0804-Y30R «S 0804-Y30R» | 5: 32,8 | 32,8 |
| О14 | окраска Tikkurila · No. 93 «Studio Green — почти чёрный зелёный» | 5: 13,1 | 13,1 |
| О16 | окраска Tikkurila · No. 105 «Slaked Lime» | 7: 25,8 | 25,8 |

| | | | | | |
|---|---|---|---|---|---|
| | | | | | Проект: Дом 331 м² |
| | Лист | № док. | Подпись | Дата | |
| Дизайнер | Кырлан А.С. | | | 19.10.26 | Карта покрытий стен · 1-й этаж |

| Стадия | Лист | Листов |
|---|---|---|
| П | 10 | 156 |

выпуск 18.10.2026 № 8cd922c868 · стр. 10 из 156

Правка к этому листу

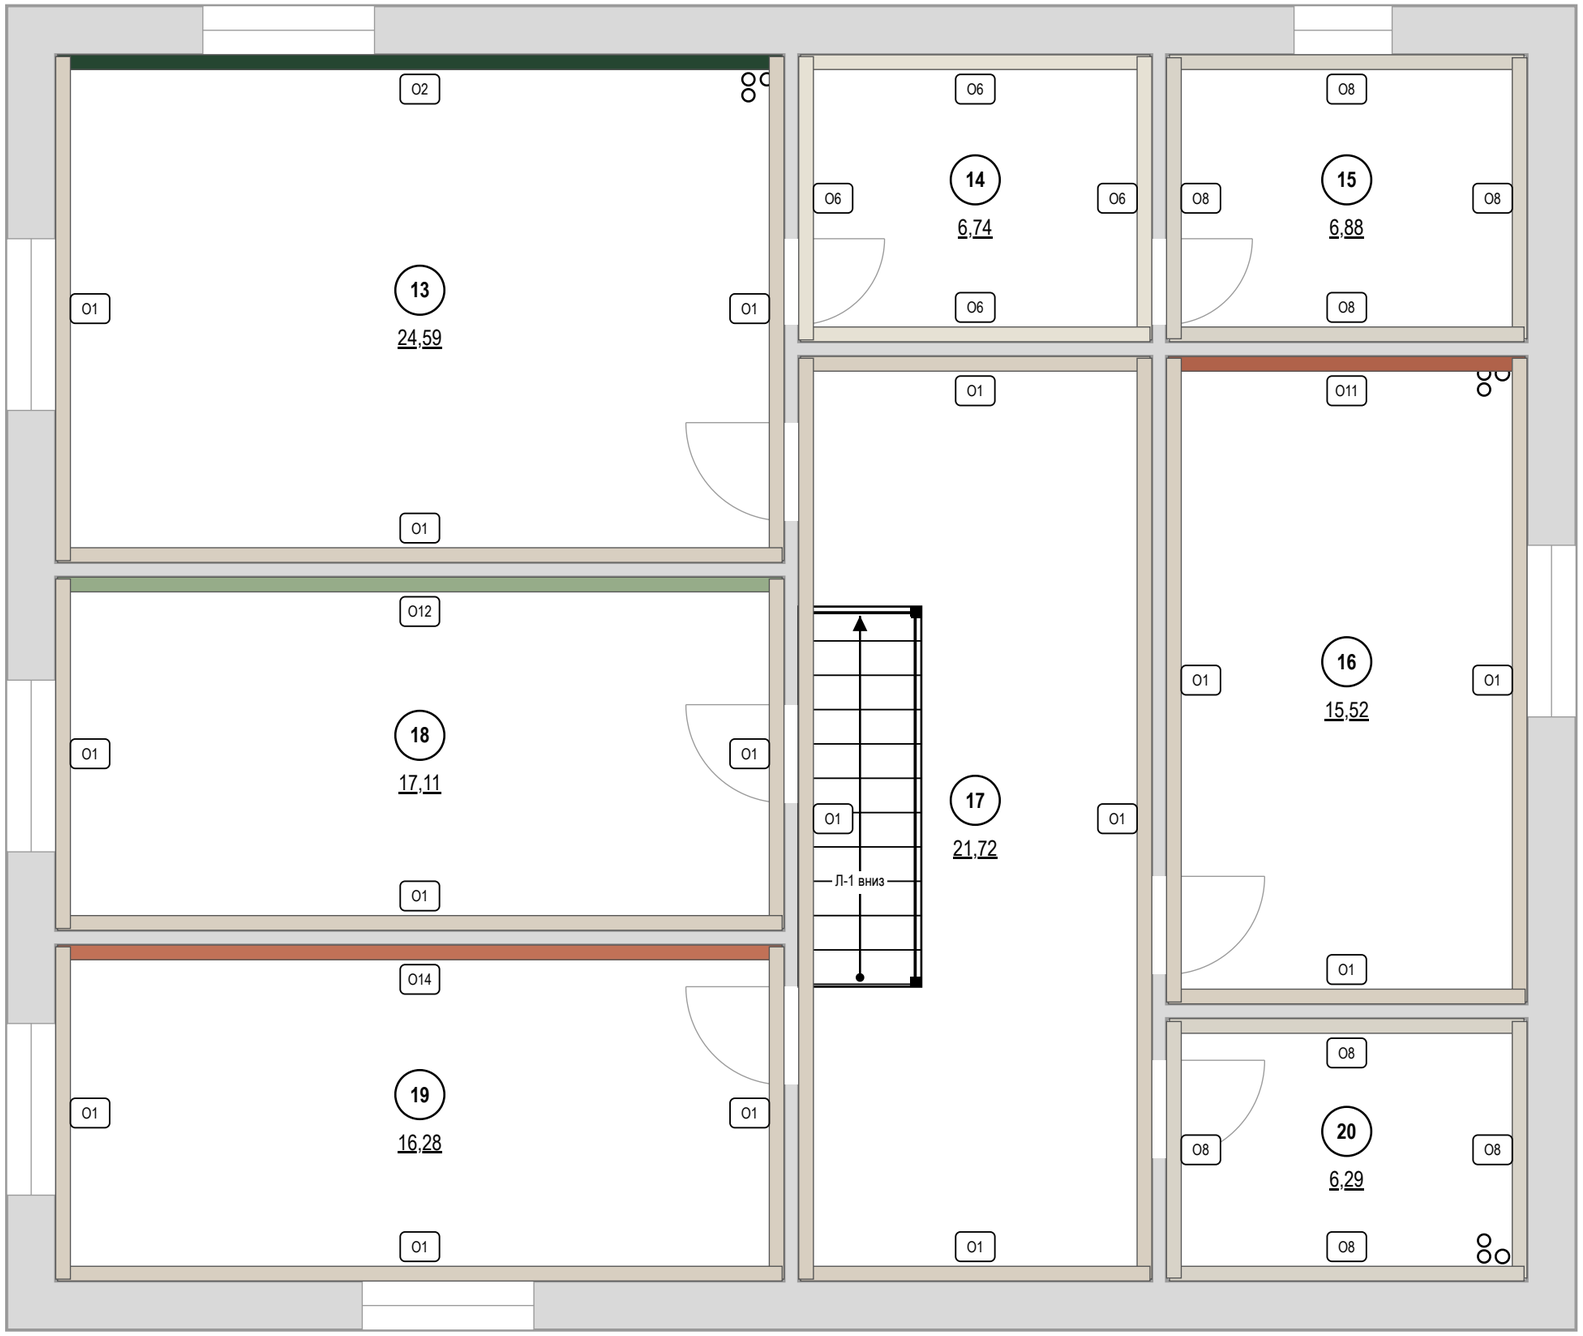


## Покрытия стен

| Марка | Покрытие | Помещение: S, м² | Итого, м² |
|---|---|---|---|
| О1 | окраска Farrow & Ball · No. 226 «Joa's White» | 13: 30,1; 16: 29,7; 17: 45,5; 18: 25,2; 19: 22,4 | 153,0 |
| О2 | окраска Farrow & Ball · S 7020-G10Y «Хвойный тёмно-зелёный» | 13: 12,7 | 12,7 |
| О6 | окраска Tikkurila · No. 105 «Slaked Lime» | 14: 24,9 | 24,9 |
| О8 | облицовка плиткой Atlas Concorde · A8UZ «Marvel Travertine» 600×1200 мм | 15: 22,8; 20: 22,3 | 45,1 |

| | | | | | |
|---|---|---|---|---|---|
| | | | | | Проект: Дом 331 м² |
| | Лист | № док. | Подпись | Дата | |
| Дизайнер | Кырлан А.С. | | | 19.10.26 | Карта покрытий стен · Мансарда |

| Стадия | Лист | Листов |
|---|---|---|
| П | 11 | 156 |

выпуск 18.10.2026 № 8cd922c868 · стр. 11 из 156

Правка к этому листу

## Колерная карта по помещениям

| Помещение | Поверхность | Образец | Поз. | Система и код цвета | Производитель, линейка / материал, артикул | Блеск | Класс EN 13300 | LRV | Площадь |
|---|---|---|---|---|---|---|---|---|---|
| **1. Кухня-столовая** 24,59 м² | стены | | **К1** | NCS S 0804-Y30R | Tikkurila · Luja 7 | полуматов. | 1 | 85 | 45,0 м² |
| | потолок | | **К2** | NCS S 0804-Y30R | Tikkurila · Luja 7 | матовая | 1 | 85 | 24,6 м² |
| | пол | | **КМ1** | по образцу | Coswick · Вековые традиции | | | | 24,6 м² |
| | плинтус | | **К3** | NCS S 0804-Y30R | МДФ · в цвет NCS | полуглянц. | 2 | 85 | 18,3 м |
| | фартук | | **КМ2** | тон Paper F497 (тёплый белый) | керамогранит · аналог по хар. | | | | 0,9 м² |
| **2. Кабинет-гостевая** 11,92 м² | стены | | **К4** | Farrow & Ball No. 226 | Farrow & Ball · Modern Emulsion | матовая | 1 | 63 | 24,7 м² |
| | акцент А | | **К5** | Farrow & Ball No. 298 | Farrow & Ball · Modern Emulsion | матовая | 1 | 14 | 5,5 м² |
| | потолок | | **К6** | Little Greene No. 105 | Tikkurila · Anti-Reflex 2 | глубокомат. | 2 | 82 | 11,9 м² |
| | пол | | **КМ1** | по образцу | Coswick · Вековые традиции | | | | 11,9 м² |
| | плинтус | | **К7** | Farrow & Ball No. 226 | МДФ · в цвет Farrow & Ball | | | 63 | 11,7 м |
| **3. Санузел 1 этажа** 4,87 м² | стены | | **К8** | Atlas Concorde A8UZ | Atlas Concorde · Marvel Travertine | | | | 20,5 м² |
| | потолок | | **К9** | Little Greene No. 105 | Tikkurila · Luja 7 | матовая | 1 | 82 | 4,9 м² |
| | пол | | **К8** | Atlas Concorde A8UZ | Atlas Concorde · Marvel Travertine | | | | 4,9 м² |
| **4. Котельная** 6,88 м² | стены | | **К4** | Farrow & Ball No. 226 | Farrow & Ball · Modern Emulsion | матовая | 1 | 63 | 27,0 м² |
| | потолок | | **К6** | Little Greene No. 105 | Tikkurila · Anti-Reflex 2 | глубокомат. | 2 | 82 | 6,9 м² |
| | пол | | **К8** | Atlas Concorde A8UZ | Atlas Concorde · Marvel Travertine | | | | 6,9 м² |
| | плинтус | | **К7** | Farrow & Ball No. 226 | МДФ · в цвет Farrow & Ball | | | 63 | 9,7 м |
| **5. Гостиная** 33,74 м² | стены | | **К10** | NCS S 0804-Y30R | Tikkurila · Optiva 5 Matt | матовая | 2 | 85 | 33,1 м² |
| | акцент А | | **К11** | Farrow & Ball No. 93 | Tikkurila · Optiva 5 Matt | матовая | 2 | 7 | 13,2 м² |
| | потолок | | **К12** | NCS S 0804-Y30R | Tikkurila · Anti-Reflex 2 | глубокомат. | 2 | 85 | 33,7 м² |
| | пол | | **КМ1** | по образцу | Coswick · Вековые традиции | | | | 33,7 м² |
| | плинтус | | **К3** | NCS S 0804-Y30R | МДФ · в цвет NCS | полуглянц. | 2 | 85 | 18,2 м |
| **6. Холл с лестницей** 10,02 м² | стены | | **К4** | Farrow & Ball No. 226 | Farrow & Ball · Modern Emulsion | матовая | 1 | 63 | 22,3 м² |
| | потолок | | **К6** | Little Greene No. 105 | Tikkurila · Anti-Reflex 2 | глубокомат. | 2 | 82 | 10,0 м² |
| | пол | | **КМ1** | по образцу | Coswick · Вековые традиции | | | | 10,0 м² |
| | плинтус | | **К7** | Farrow & Ball No. 226 | МДФ · в цвет Farrow & Ball | | | 63 | 7,0 м |
| **7. Кладовая** 5,99 м² | стены | | **К13** | Little Greene No. 105 | Tikkurila · Harmony | матовая | 1 | 82 | 23,3 м² |
| | потолок | | **К6** | Little Greene No. 105 | Tikkurila · Anti-Reflex 2 | глубокомат. | 2 | 82 | 6,0 м² |
| | пол | | **КМ1** | по образцу | Coswick · Вековые традиции | | | | 6,0 м² |
| | плинтус | | **К14** | Little Greene No. 105 | МДФ · в цвет Little Greene | | | 82 | 7,8 м |
| **8. Прихожая** 12,46 м² | стены | | **К4** | Farrow & Ball No. 226 | Farrow & Ball · Modern Emulsion | матовая | 1 | 63 | 39,0 м² |
| | потолок | | **К6** | Little Greene No. 105 | Tikkurila · Anti-Reflex 2 | глубокомат. | 2 | 82 | 12,5 м² |
| | пол | | **К8** | Atlas Concorde A8UZ | Atlas Concorde · Marvel Travertine | | | | 12,5 м² |
| | плинтус | | **К7** | Farrow & Ball No. 226 | МДФ · в цвет Farrow & Ball | | | 63 | 13,6 м |
| **9. Тамбур** 3,49 м² | стены | | **К4** | Farrow & Ball No. 226 | Farrow & Ball · Modern Emulsion | матовая | 1 | 63 | 17,1 м² |
| | потолок | | **К6** | Little Greene No. 105 | Tikkurila · Anti-Reflex 2 | глубокомат. | 2 | 82 | 3,5 м² |
| | пол | | **К8** | Atlas Concorde A8UZ | Atlas Concorde · Marvel Travertine | | | | 3,5 м² |
| | плинтус | | **К7** | Farrow & Ball No. 226 | МДФ · в цвет Farrow & Ball | | | 63 | 5,6 м |
| **10. Гараж** 41,58 м² | стены | | **К4** | Farrow & Ball No. 226 | Farrow & Ball · Modern Emulsion | матовая | 1 | 63 | 62,6 м² |
| | потолок | | **К6** | Little Greene No. 105 | Tikkurila · Anti-Reflex 2 | глубокомат. | 2 | 82 | 41,6 м² |
| | пол | | **КМ3** | по образцу | ероху · аналог по хар. | | | | 41,6 м² |
| | плинтус | | **КМ4** | по образцу | pvc · аналог по хар. | | | | 22,0 м |

## Примечания

1. Цвет утверждается только по выкрасу на объекте: формат от А3 до 1000×1000 мм на загрунтованном ГКЛ, в 2 слоя (как на стене), не на белой шпаклёвке; смотреть днём и при свете проекта своего помещения, рядом с образцами пола и фасадов. Подпись на обороте: код, бренд и веер, дата.
2. Колеровка машинная в колеровочном центре бренда; каждый код — за один проход, одной партией на весь объём. Колеровщику передаётся только система и код утверждённого веера; плашки и HEX на листе — ориентир, печать не является эталоном цвета.
3. Класс мокрого истирания — EN 13300 (ISO 11998); блеск — по ГОСТ 31975 (ISO 2813), геометрия 60°. LRV — пересчёт координаты L каталога производителя (Y = ((L*+16)/116)³); «≈» — расчёт по HEX, справочно.
4. Площади поверхностей — тем же способом и с теми же цифрами, что в ведомости отделки (способ счёта — в общих указаниях); объём краски к заказу, фасовка и материалы КМ — в спецификации отделочных материалов.
5. Колерная карта на 2 листах: обозначения повторены на каждом, схема квартиры и палитра — на первом, перечень выкрасов — на последнем.

## Схема палитры проекта

Стиль: Шале 60% + Эко и органический модерн 40% · схема: complement

| основной Farrow & Ball No. 226 | основной NCS S 0804-Y30R | основной Little Greene No. 105 | второстепенный Tikkurila V451 | второстепенный NCS S 3020-G30Y | второстепенный Tikkurila X463 | второстепенный Farrow & Ball No. 223 | второстепенный Farrow & Ball No. 88 | второстепенный Farrow & Ball No. 245 | второстепенный NCS S 2005-Y20R | второстепенный NCS S 3010-Y30R | акцентный NCS S 7020-G10Y | акцентный Farrow & Ball No. 64 | акцентный Farrow & Ball No. 43 |
|---|---|---|---|---|---|---|---|---|---|---|---|---|---|
| Joa's White LRV 63 стены 2,4,6,8,9,10,13,16,17,18,19; плинтус 1,4,6,8,9,10,11,17,20 по последнему 20.11 | тёплый молочный белый LRV 85 стены 1,5,11,12; потолок 1,5,11,12 потолок 1 стандарт, 5 по последнему 25.11 | Slaked Lime LRV 82 потолок 2,3,4,6,7,8,9,10,13,14,15,16,18,19,20 стены 7,14 стандарт, 17,21 по последнему 20.11 | Olive grove V451 LRV 51 текстиль/декор 18 | шалфей LRV 38 акцент 18; текстиль/декор 17,18 | Sandstone X463 LRV 51 текстиль/декор 2,16,19 | Elephant's foot LRV 52 текстиль/декор 13 | Mouse's foot LRV 26 текстиль/декор 2 | Charleston Grey LRV 30 текстиль/декор 5,10 | Светлый песочно-серый LRV 60 текстиль/декор 1,5,13,18,19 | орех/лён тёмный LRV 43 текстиль/декор 2,16,19 | Хвойный тёмно-зелёный LRV ≈5 акцент 13; текстиль/декор 13 | Red Earth LRV 18 акцент 16; текстиль/декор 16 | Eating Room Red LRV 11.8 в отделке не применён |

План 60/30/10

Окраска, факт — по площади стен, акцентов, потолков

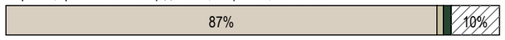


окрашено всего 940,2 м²; второстепенный тон несут мебель и текстиль

## Условные обозначения

- **К1** NCS S 0804-Y30R · тёплый молочный белый · Tikkurila Luja 7 · полуматов. · кл. 1
- **К2** NCS S 0804-Y30R · тёплый молочный белый · Tikkurila Luja 7 · матовая · кл. 1
- **К3** NCS S 0804-Y30R · тёплый молочный белый · МДФ · полуглянц. · кл. 2
- **К4** Farrow & Ball No. 226 · Joa's White · Modern Emulsion · матовая · кл. 1
- **К5** Farrow & Ball No. 298 · Bancha · Modern Emulsion · матовая · кл. 1
- **К6** Little Greene No. 105 · Slaked Lime · Anti-Reflex 2 · глубокомат. · кл. 2
- **К7** Farrow & Ball No. 226 · Joa's White · МДФ
- **К8** Atlas Concorde A8UZ · Marvel Travertine · Marvel Travertine
- **К9** Little Greene No. 105 · Slaked Lime · Luja 7 · матовая · кл. 1
- **К10** NCS S 0804-Y30R · тёплый молочный белый · Tikkurila Optiva 5 Matt · матовая · кл. 2
- **К11** Farrow & Ball No. 93 · Studio Green — почти чёрный зелёный · Optiva 5 Matt · матовая · кл. 2
- **К12** NCS S 0804-Y30R · тёплый молочный белый · Tikkurila Anti-Reflex 2 · глубокомат. · кл. 2
- **К13** Little Greene No. 105 · Slaked Lime · Harmony · матовая · кл. 1
- **К14** Little Greene No. 105 · Slaked Lime · МДФ
- **К15** NCS S 7020-G10Y · Хвойный тёмно-зелёный · Farrow & Ball Modern Emulsion · матовая · кл. 1
- **К16** Farrow & Ball No. 64 · Red Earth · Modern Emulsion · матовая · кл. 1
- **К17** NCS S 3020-G30Y · шалфей · Farrow & Ball Modern Emulsion · матовая · кл. 1
- **К18** Farrow & Ball No. 226 · Joa's White · Contour (Luxxus)
- **К19** NCS S 3040-Y70R · обожжённая глина · Farrow & Ball Modern Emulsion · матовая · кл. 1
- **КМ1** инженерная доска · 1167-4250
- **КМ2** аналог: керамогранит матовый, тон F497, 600×600×9 мм
- **КМ3** ероху · аналог: наливной полимерный пол (эпоксидный), с кварцевой посыпкой, 3 мм
- **КМ4** pvc · аналог: плинтус ПВХ влагостойкий 100 мм, серый
- **КМ5** керамогранит · A8UZ
- **КМ6** керамогранит · аналог: плинтус из керамогранита пола, подрезка 80 мм, верхняя кромка с запилом 45°

дерево (доска, паркет, ламинат) — рисунок досок

керамогранит, плитка, камень — сетка швов по формату

материал без кода цвета — по образцу (артикул в ведомости отделки)

HEX не задан — цвет только по коду и вееру

К — позиция окраски (код + продукт + блеск), КМ — позиция материала, тон КМ — по описанию артикула, эталон — образец материала; ≈ LRV — расчёт по HEX, справочно

| | | | | | |
|---|---|---|---|---|---|
| | | | | | Проект: Дом 331 м² |
| | Лист | № док. | Подпись | Дата | |
| Дизайнер | Кырлан А.С. | | | 19.10.26 | Колерная карта |

| Стадия | Лист | Листов |
|---|---|---|
| П | 12 | 156 |

выпуск 18.10.2026 № 8cd922c868 · стр. 12 из 156

Правка к этому листу

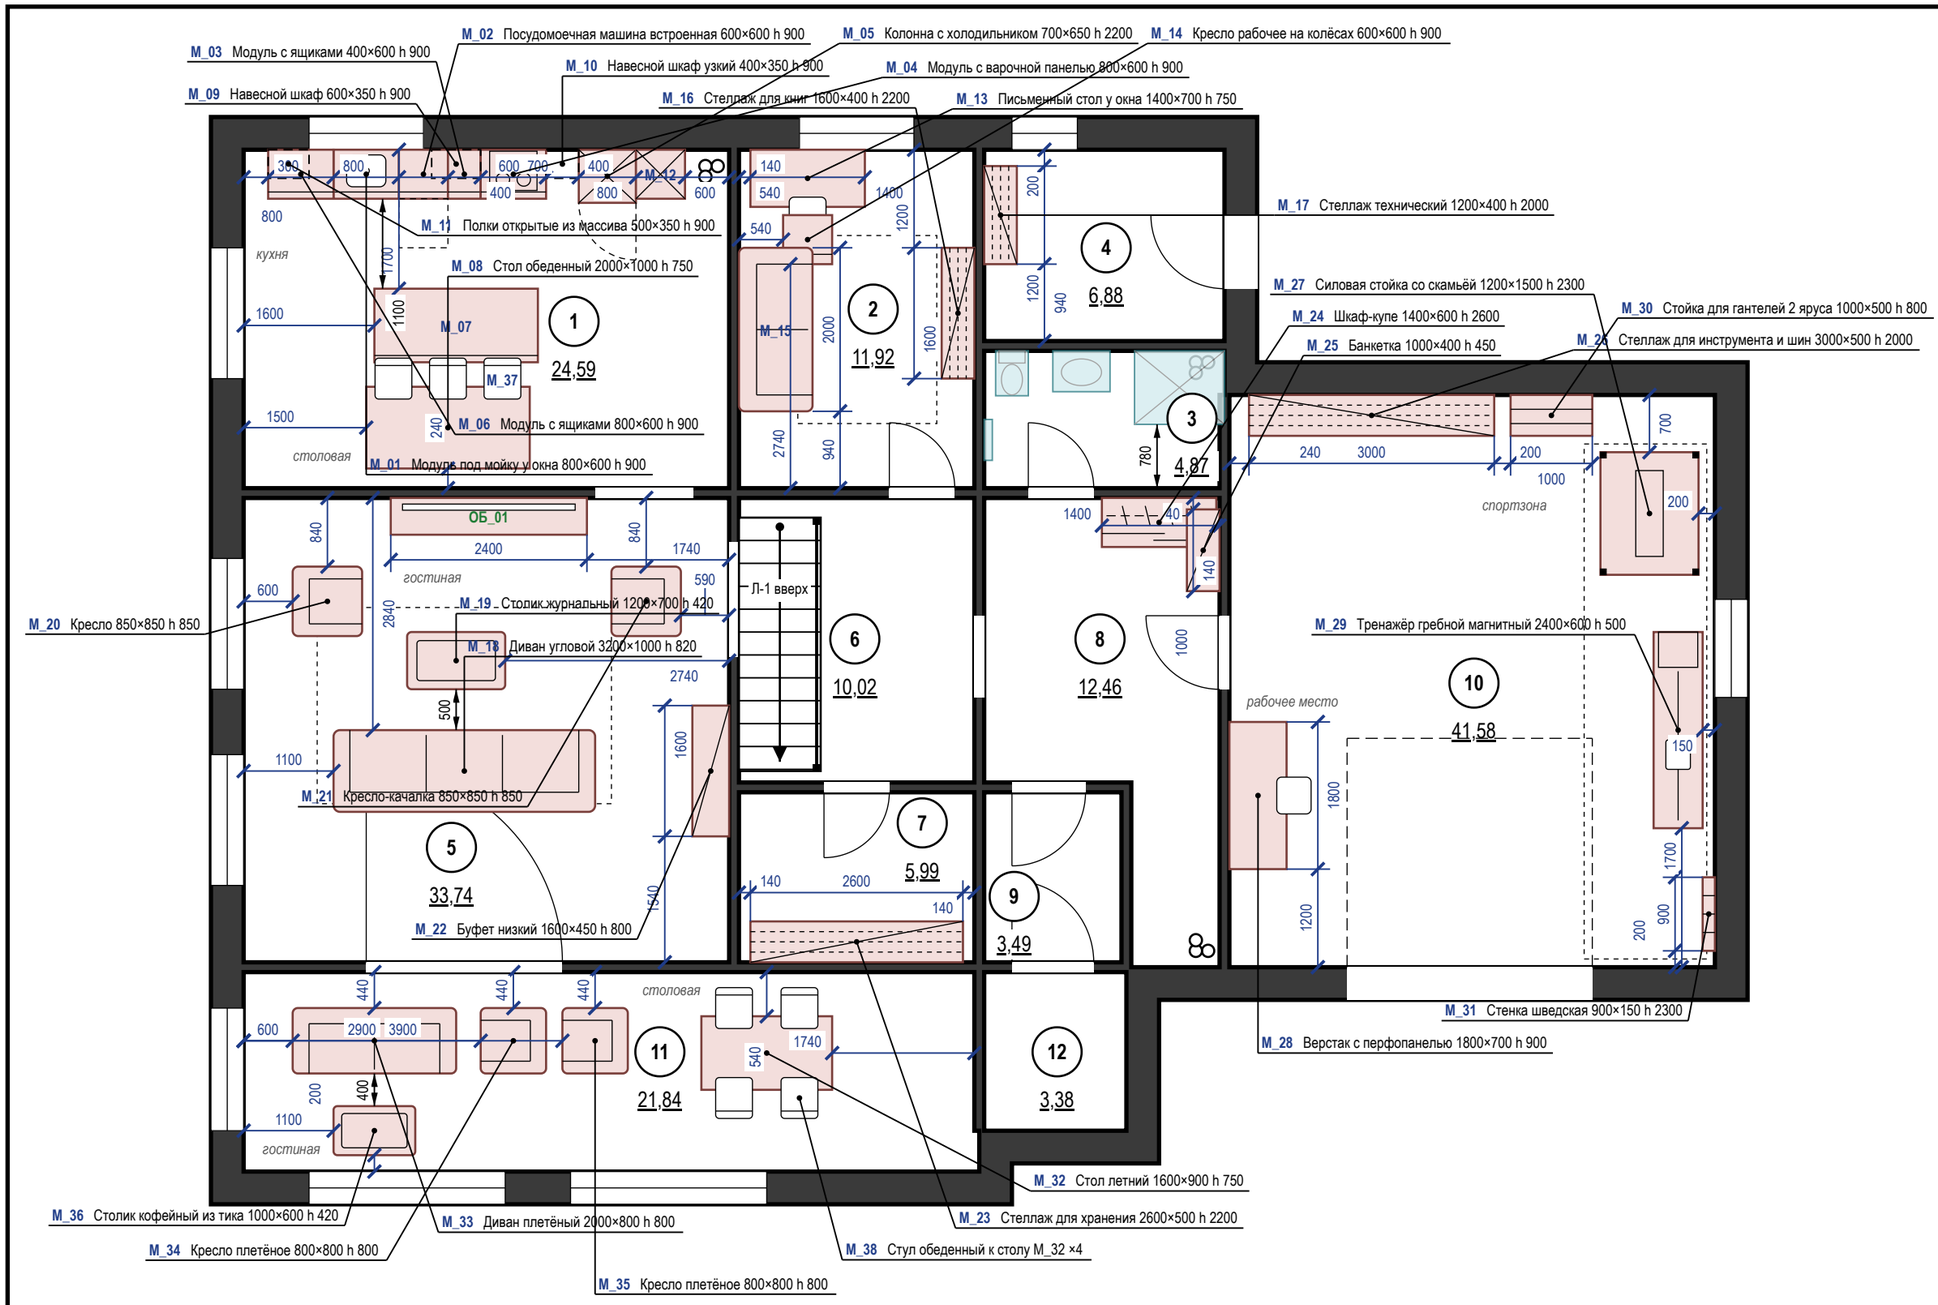


## Примечания

1. Размеры — в мм от чистовых поверхностей стен; размеры мебели уточнить после отделочных работ; общие указания — лист 2.
2. Стулья обеденной группы (M_37 — 3 шт., M_38 — 4 шт.) показаны в рабочем положении, задвинутыми под столешницу на 150 мм.

**Экспликация помещений**

лист обмерного плана · на плане — номера в марках

## Ведомость мебели и оборудования

| Марка | Наименование | Ш×Г×В, мм | Пом. | Кол. |
|---|---|---|---|---|
| M_01 | Модуль под мойку у окна | 800×600×900 | 1 | 1 |
| M_02 | Посудомоечная машина встроенная | 600×600×900 | 1 | 1 |
| M_03 | Модуль с ящиками | 400×600×900 | 1 | 1 |
| M_04 | Модуль с варочной панелью | 800×600×900 | 1 | 1 |
| M_05 | Колонна с холодильником | 700×650×2200 | 1 | 1 |
| M_06 | Модуль с ящиками | 800×600×900 | 1 | 1 |
| M_07 | Остров с барной консолью | 2000×900×900 | 1 | 1 |
| M_08 | Стол обеденный 2000×1000 | 2000×1000×750 | 1 | 1 |
| M_09 | Навесной шкаф | 600×350×900 | 1 | 1 |
| M_10 | Навесной шкаф узкий | 400×350×900 | 1 | 1 |
| M_11 | Полки открытые из массива | 500×350×900 | 1 | 1 |
| M_12 | Пенал-кладовая с выдвижными корзинами | 600×600×2200 | 1 | 1 |
| M_13 | Письменный стол у окна | 1400×700×750 | 2 | 1 |
| M_14 | Кресло рабочее на колёсах | 600×600×900 | 2 | 1 |
| M_15 | Диван-кровать гостевой | 2000×900×850 | 2 | 1 |
| M_16 | Стеллаж для книг | 1600×400×2200 | 2 | 1 |
| M_17 | Стеллаж технический | 1200×400×2000 | 4 | 1 |
| ОБ_01 | ТВ-стена с камином | 2400×450×600 | 5 | 1 |
| M_18 | Диван угловой | 3200×1000×820 | 5 | 1 |
| M_19 | Столик журнальный | 1200×700×420 | 5 | 1 |
| M_20 | Кресло | 850×850×850 | 5 | 1 |
| M_21 | Кресло-качалка | 850×850×850 | 5 | 1 |
| M_22 | Буфет низкий | 1600×450×800 | 5 | 1 |
| M_23 | Стеллаж для хранения | 2600×500×2200 | 7 | 1 |
| M_24 | Шкаф-купе | 1400×600×2600 | 8 | 1 |
| M_25 | Банкетка | 1000×400×450 | 8 | 1 |
| M_26 | Стеллаж для инструмента и шин | 3000×500×2000 | 10 | 1 |
| M_27 | Силовая стойка со скамьёй | 1200×1500×2300 | 10 | 1 |
| M_28 | Верстак с перфопанелью | 1800×700×900 | 10 | 1 |
| M_29 | Тренажёр гребной магнитный | 2400×600×500 | 10 | 1 |
| M_30 | Стойка для гантелей 2 яруса | 1000×500×800 | 10 | 1 |
| M_31 | Стенка шведская | 900×150×2300 | 10 | 1 |
| M_32 | Стол летний | 1600×900×750 | 11 | 1 |
| M_33 | Диван плетёный | 2000×800×800 | 11 | 1 |
| M_34 | Кресло плетёное | 800×800×800 | 11 | 1 |
| M_35 | Кресло плетёное | 800×800×800 | 11 | 1 |
| M_36 | Столик кофейный из тика | 1000×600×420 | 11 | 1 |
| M_37 | Стул обеденный к столу M_08 | 450×500×820 | 1 | 3 |
| M_38 | Стул обеденный к столу M_32 | 450×500×820 | 11 | 4 |

Ш — вдоль стены (изголовья), Г — от стены (длина кровати)

Материалы, модели, допуск замены — лист 15

| | | | | | |
|---|---|---|---|---|---|
| | Лист | № док. | Подпись | Дата | Проект: Дом 331 м² |
| Дизайнер | Кырлан А.С. | | | 19.10.26 | План размещения мебели и оборудования · 1-й этаж |

| Стадия | Лист | Листов |
|---|---|---|
| П | 13 | 156 |

выпуск 18.10.2026 № 8cd922c868 · стр. 13 из 156

Правка к этому листу

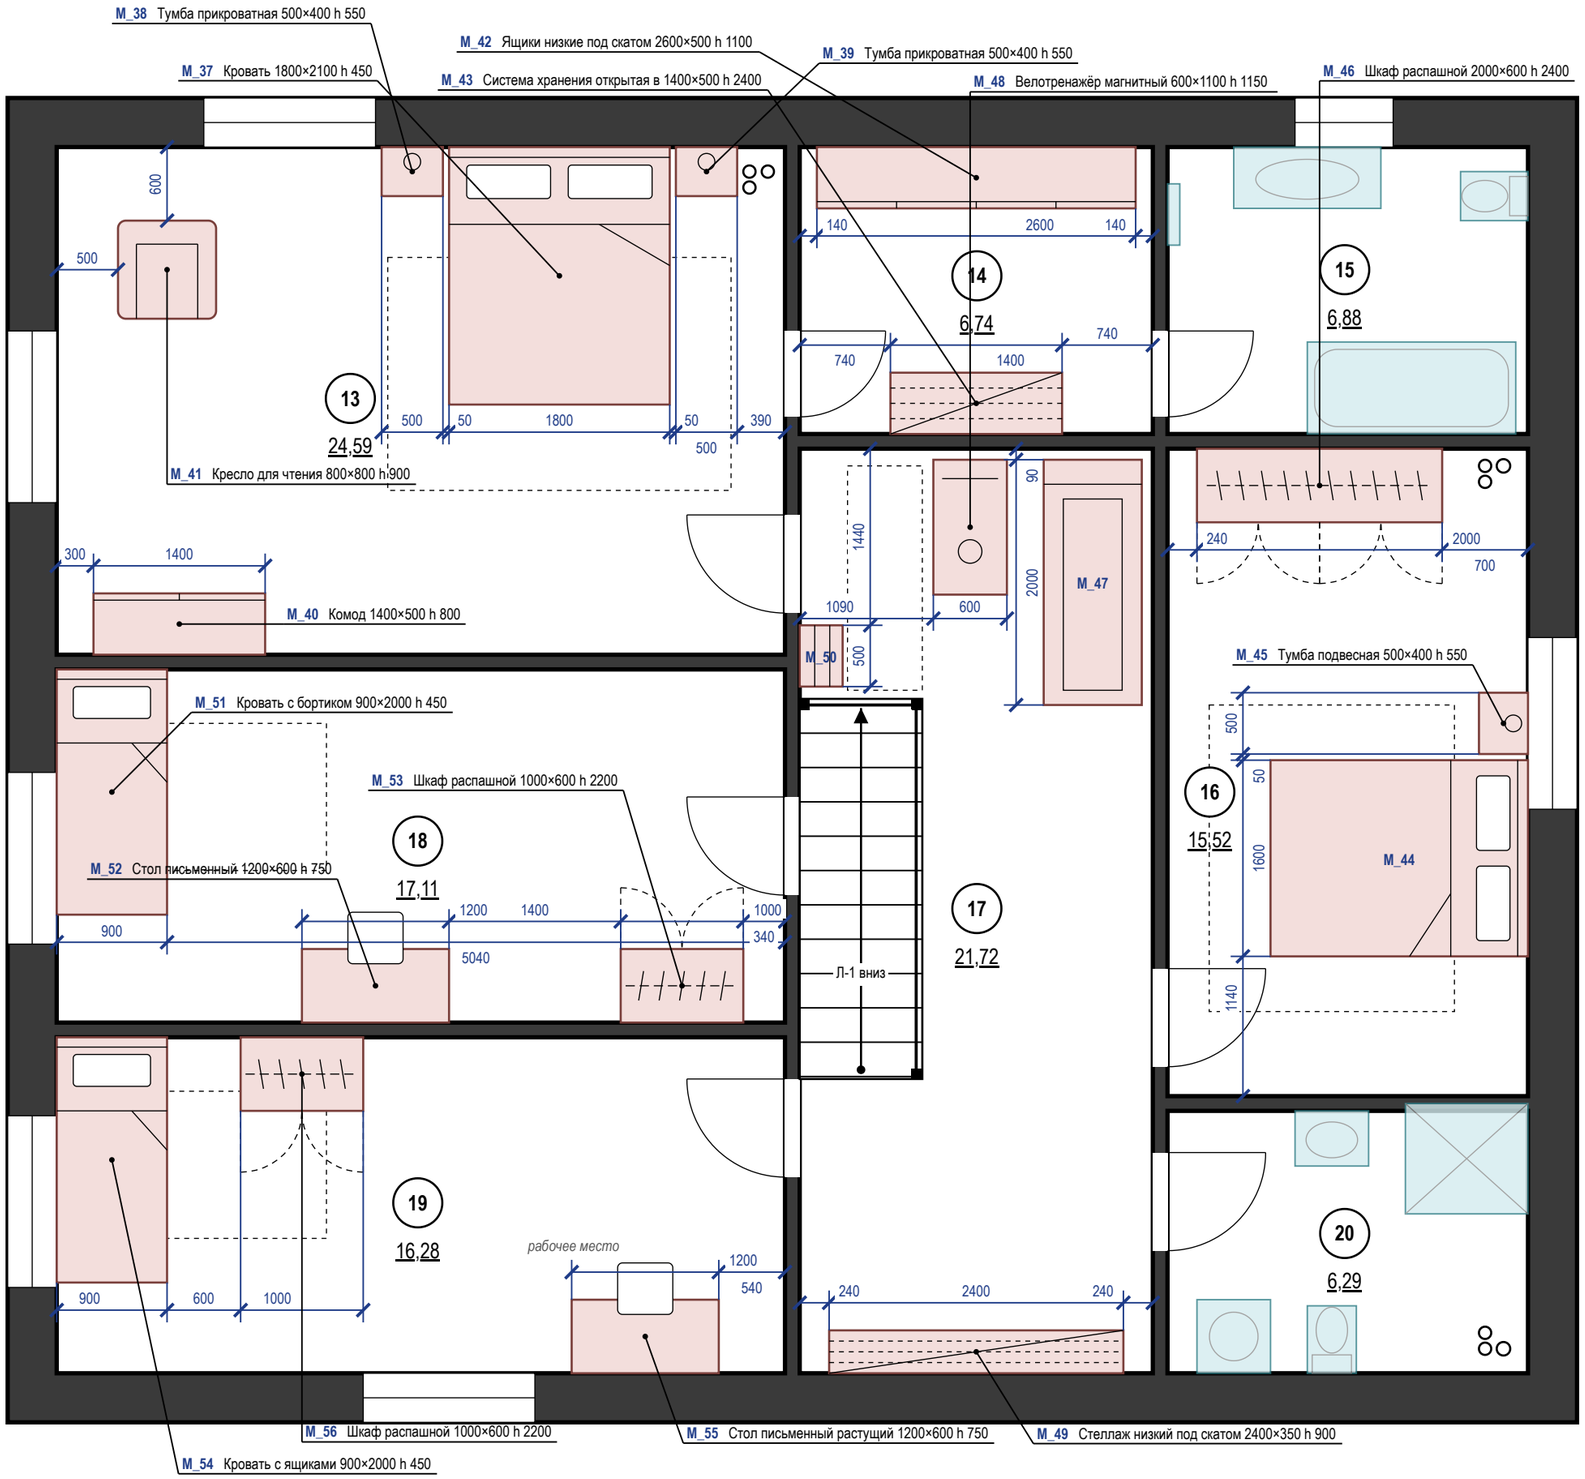


**Экспликация помещений**

лист обмерного плана · на плане — номера в марках

## Ведомость мебели и оборудования

| Марка | Наименование | Ш×Г×В, мм | Пом. | Кол. |
|---|---|---|---|---|
| M_37 | Кровать 1800×2000 | 1800×2100×450 | 13 | 1 |
| M_38 | Тумба прикроватная | 500×400×550 | 13 | 1 |
| M_39 | Тумба прикроватная | 500×400×550 | 13 | 1 |
| M_40 | Комод | 1400×500×800 | 13 | 1 |
| M_41 | Кресло для чтения | 800×800×900 | 13 | 1 |
| M_42 | Ящики низкие под скатом | 2600×500×1100 | 14 | 1 |
| M_43 | Система хранения открытая в | 1400×500×2400 | 14 | 1 |
| M_44 | Кровать 1600×2000 | 1600×2100×450 | 16 | 1 |
| M_45 | Тумба подвесная | 500×400×550 | 16 | 1 |
| M_46 | Шкаф распашной | 2000×600×2400 | 16 | 1 |
| M_47 | Дорожка беговая складная | 2000×800×1400 | 17 | 1 |
| M_48 | Велотренажёр магнитный | 600×1100×1150 | 17 | 1 |
| M_49 | Стеллаж низкий под скатом | 2400×350×900 | 17 | 1 |
| M_50 | Стойка-этажерка для инвентаря | 500×350×1000 | 17 | 1 |
| M_51 | Кровать 900×2000 с бортиком | 900×2000×450 | 18 | 1 |
| M_52 | Стол письменный | 1200×600×750 | 18 | 1 |
| M_53 | Шкаф распашной | 1000×600×2200 | 18 | 1 |
| M_54 | Кровать 900×2000 с ящиками | 900×2000×450 | 19 | 1 |
| M_55 | Стол письменный растущий | 1200×600×750 | 19 | 1 |
| M_56 | Шкаф распашной | 1000×600×2200 | 19 | 1 |

Ш — вдоль стены (изголовья), Г — от стены (длина кровати)

Материалы, модели, допуск замены — лист 15

## Примечания

1. Размеры — в мм от чистовых поверхностей стен; размеры мебели уточнить после отделочных работ; общие указания — лист 2.
2. Отступ от стены, на плане не образмерен: M_47 — 90 мм, M_48 — 90 мм.

| | | | | |
|---|---|---|---|---|
| | Лист | № док. | Подпись | Дата |
| Дизайнер | Кырлан А.С. | | | 19.10.26 |

Проект: Дом 331 м²

План размещения мебели и оборудования · Мансарда

| Стадия | Лист | Листов |
|---|---|---|
| П | 14 | 156 |

выпуск 18.10.2026 № 8cd922c868 · стр. 14 из 156

Правка к этому листу

| Поз. | Наименование и техническая характеристика | Тип, марка, обозначение документа, опросного листа | Код продукции | Поставщик | Ед. измерения | Кол. | Масса 1 ед., кг | Примечание |
|---|---|---|---|---|---|---|---|---|
| | **Мебель встроенная и корпусная (изготовление по чертежам мебельщика)** | | | | | | | |
| M_01 | Модуль под мойку у окна; корпус ЛДСП, фасады — матовая эмаль в тон стен; Ш×Г×В 800×600×900 мм | | | изготовление на заказ | шт. | 1 | | пом. 1 |
| M_02 | Посудомоечная машина встроенная; корпус ЛДСП, фасады — матовая эмаль в тон стен; Ш×Г×В 600×600×900 мм | | | изготовление на заказ | шт. | 1 | | пом. 1 |
| M_03 | Модуль с ящиками; корпус ЛДСП, фасады — матовая эмаль в тон стен; Ш×Г×В 400×600×900 мм | | | изготовление на заказ | шт. | 1 | | пом. 1 |
| M_04 | Модуль с варочной панелью и духовым шкафом; корпус ЛДСП, фасады — матовая эмаль в тон стен; Ш×Г×В 800×600×900 мм | | | изготовление на заказ | шт. | 1 | | пом. 1 |
| M_05 | Колонна с холодильником; корпус ЛДСП, фасады — матовая эмаль в тон стен; Ш×Г×В 700×650×2200 мм | | | изготовление на заказ | шт. | 1 | | пом. 1 |
| M_06 | Модуль с ящиками; корпус ЛДСП, фасады — матовая эмаль в тон стен; Ш×Г×В 800×600×900 мм | | | изготовление на заказ | шт. | 1 | | пом. 1 |
| M_07 | Остров с барной консолью из массива дуба, столешница — кварц; корпус ЛДСП, фасады — рейка из массива дуба, столешница — кварцевый агломерат 20 мм, консоль для завтрака — массив дуба 40 мм; Ш×Г×В 2000×900×900 мм | | | изготовление на заказ | шт. | 1 | | пом. 1 |
| M_09 | Навесной шкаф, фасад в тон острова; корпус ЛДСП, фасады — матовая эмаль в тон стен; Ш×Г×В 600×350×900 мм | | | изготовление на заказ | шт. | 1 | | пом. 1 |
| M_10 | Навесной шкаф узкий, полки для специй; корпус ЛДСП, фасады — матовая эмаль в тон стен; Ш×Г×В 400×350×900 мм | | | изготовление на заказ | шт. | 1 | | пом. 1 |
| M_11 | Полки открытые из массива дуба у окна, 3 яруса; полки — массив дуба 30 мм, масло; кронштейны — чёрная сталь; Ш×Г×В 500×350×900 мм | | | изготовление на заказ | шт. | 1 | | пом. 1 |
| M_12 | Пенал-кладовая с выдвижными корзинами; корпус ЛДСП, фасады — матовая эмаль в тон стен; Ш×Г×В 600×600×2200 мм | | | изготовление на заказ | шт. | 1 | | пом. 1 |
| M_24 | Шкаф-купе, светлый дуб; корпус ЛДСП, фасады — матовая эмаль в цвет стен (Farrow & Ball No. 226); Ш×Г×В 1400×600×2600 мм | | | изготовление на заказ | шт. | 1 | | пом. 8 |
| M_46 | Шкаф распашной, фасады — шпон ясеня с вертикальной рейкой; корпус ЛДСП, фасады — шпон ясеня с вертикальной рейкой, масло; Ш×Г×В 2000×600×2400 мм | | | изготовление на заказ | шт. | 1 | | пом. 16 |
| M_53 | Шкаф распашной, фасады — матовая эмаль шалфей; корпус ЛДСП, фасады МДФ — матовая эмаль NCS S 3020-G30Y; Ш×Г×В 1000×600×2200 мм | | | изготовление на заказ | шт. | 1 | | пом. 18 |
| M_56 | Шкаф распашной (вне ската), фасады — дуб и эмаль терракота; корпус ЛДСП, фасады — шпон дуба и МДФ в матовой эмали NCS S 3040-Y70R; Ш×Г×В 1000×600×2200 мм | | | изготовление на заказ | шт. | 1 | | пом. 19 |
| | **Мебель покупная** | | | | | | | |
| M_08 | Стол обеденный 2000×1000, массив дуба; шпон, дуб натуральный, матовое масло; Ш×Г×В 2000×1000×750 мм | | | аналог по характеристикам | шт. | 1 | | пом. 1; замена ≤ габарита |
| M_57 | Стул обеденный к столу M_08; обивка — ткань, цвет Tikkurila V451; каркас — дуб натуральный; Ш×Г×В 450×500×820 мм | | | аналог по характеристикам | шт. | 3 | | пом. 1; замена ≤ габарита |
| M_13 | Письменный стол у окна, массив дуба на чёрном стальном подстолье; дерево — дуб массив, масло, металл — чёрный матовый; Ш×Г×В 1400×700×750 мм | | | аналог по характеристикам | шт. | 1 | | пом. 2; замена ≤ габарита |
| M_14 | Кресло рабочее на колёсах, кожа коньячная; обивка кожа натуральная, коньяк; Ш×Г×В 600×600×900 мм | | | аналог по характеристикам | шт. | 1 | | пом. 2; замена ≤ габарита |
| M_15 | Диван-кровать гостевой, шерстяной твид; обивка шерстяной твид, серо-оливковый меланж; Ш×Г×В 2000×900×850 мм | | | аналог по характеристикам | шт. | 1 | | пом. 2; замена ≤ габарита |
| M_16 | Стеллаж для книг, чёрная сталь и полки из дуба; каркас — чёрная сталь, полки — массив дуба; Ш×Г×В 1600×400×2200 мм | | | аналог по характеристикам | шт. | 1 | | пом. 2; крепление к стене; замена ≤ габарита |
| M_17 | Стеллаж технический; каркас и полки — ЛДСП, декор «дуб натуральный»; Ш×Г×В 1200×400×2000 мм | | | аналог по характеристикам | шт. | 1 | | пом. 4; замена ≤ габарита |
| M_18 | Диван угловой, лён-рогожка; обивка лён-рогожка плотный, молочный; Ш×Г×В 3200×1000×820 мм | | | аналог по характеристикам | шт. | 1 | | пом. 5; замена ≤ габарита |
| M_19 | Столик журнальный, столешница — сланец, подстолье дуб; столешница — сланец 20 мм, подстолье — массив дуба; Ш×Г×В 1200×700×420 мм | | | аналог по характеристикам | шт. | 1 | | пом. 5; замена ≤ габарита |
| M_20 | Кресло, букле (овечья шерсть); обивка букле, овечья шерсть, молочный; Ш×Г×В 850×850×850 мм | | | аналог по характеристикам | шт. | 1 | | пом. 5; замена ≤ габарита |
| M_21 | Кресло-качалка, кожа и ясень; обивка кожа натуральная, тёмный коньяк, дерево — ясень гнутый; Ш×Г×В 850×850×850 мм | | | аналог по характеристикам | шт. | 1 | | пом. 5; замена ≤ габарита |
| M_22 | Буфет низкий, дуб; шпон, дуб натуральный, матовое масло; Ш×Г×В 1600×450×800 мм | | | аналог по характеристикам | шт. | 1 | | пом. 5; крепление к стене; замена ≤ габарита |
| ОБ_01 | ТВ-стена с камином, облицовка — колотый сланец; короб ГКЛ с облицовкой колотым сланцем, полка из массива дуба; Ш×Г×В 2400×450×600 мм | | | аналог по характеристикам | шт. | 1 | | пом. 5; замена ≤ габарита |
| M_23 | Стеллаж для хранения; каркас и полки — ЛДСП, декор «дуб натуральный»; Ш×Г×В 2600×500×2200 мм | | | аналог по характеристикам | шт. | 1 | | пом. 7; замена ≤ габарита |
| M_25 | Банкетка; Ш×Г×В 1000×400×450 мм | | | аналог по характеристикам | шт. | 1 | | пом. 8; замена ≤ габарита |

## Примечания

1. Позиции мебели совпадают с марками на плане расстановки; размеры Ш×Г×В — Ш вдоль стены, Г от стены.
2. Встроенная и корпусная мебель изготавливается по чертежам мебельщика после контрольного обмера; графы «Тип, марка» и «Код продукции» для неё не заполняются (ГОСТ 21.110-2013).
3. Покупные изделия — аналог по характеристикам: заменять только на изделия не больше указанного габарита и того же материала и цвета.
4. Материал и цвет, не указанные в данных изделия, приняты по концепции: тон дерева — по полу, обивка — по вторичному цвету палитры; образцы согласовать до заказа.
5. Масса 1 ед. для изделий до 25 кг не указывается. Техника — по монтажным схемам изготовителя; выводы — по листам ЭОМ и ВК.

| | | | | | | |
|---|---|---|---|---|---|---|
| | | | | | Проект: Дом 331 м² | |
| | Лист | № док. | Подпись | Дата | Спецификация мебели и оборудования | Стадия / Лист / Листов |
| Дизайнер | Кырлан А.С. | | | 19.10.26 | | П / 15 / 156 |

Правка к этому листу

| Поз. | Наименование и техническая характеристика | Тип, марка, обозначение документа, опросного листа | Код продукции | Поставщик | Ед. измерения | Кол. | Масса 1 ед., кг | Примечание |
|---|---|---|---|---|---|---|---|---|
| M_26 | Стеллаж для инструмента и шин; каркас и полки — ЛДСП, декор «дуб натуральный»; Ш×Г×В 3000×500×2000 мм | | | аналог по характеристикам | шт. | 1 | | пом. 10; крепление к стене; замена ≤ габарита |
| M_27 | Силовая стойка со скамьёй и штангой; стальная рама, порошковая окраска, чёрный матовый; под тренажёр — резиновый коврик 10 мм; Ш×Г×В 1200×1500×2300 мм | | | аналог по характеристикам | шт. | 1 | | пом. 10; замена ≤ габарита |
| M_28 | Верстак с перфопанелью; шпон, дуб натуральный, матовое масло; Ш×Г×В 1800×700×900 мм | | | аналог по характеристикам | шт. | 1 | | пом. 10; замена ≤ габарита |
| M_29 | Тренажёр гребной магнитный, складной; алюминиевая направляющая, маховик магнитный или водяной, сиденье на роликах; под тренажёр — резиновый коврик 10 мм; Ш×Г×В 2400×600×500 мм | | | аналог по характеристикам | шт. | 1 | | пом. 10; замена ≤ габарита |
| M_30 | Стойка для гантелей 2 яруса, пары 4–20 кг; стальная рама, порошковая окраска, чёрный матовый; гантели с обрезиненными дисками; Ш×Г×В 1000×500×800 мм | | | аналог по характеристикам | шт. | 1 | | пом. 10; крепление к стене; замена ≤ габарита |
| M_31 | Стенка шведская, бук, с навесным турником; массив бука, лак матовый; перекладины Ø40 шаг 200; крепление к стене — анкеры по основанию, не менее 6; Ш×Г×В 900×150×2300 мм | | | аналог по характеристикам | шт. | 1 | | пом. 10; крепление к стене; замена ≤ габарита |
| M_32 | Стол летний; шпон, дуб натуральный, матовое масло; Ш×Г×В 1600×900×750 мм | | | аналог по характеристикам | шт. | 1 | | пом. 11; замена ≤ габарита |
| M_33 | Диван плетёный; обивка — ткань, цвет Tikkurila V451; Ш×Г×В 2000×800×800 мм | | | аналог по характеристикам | шт. | 1 | | пом. 11; замена ≤ габарита |
| M_34, M_35 | Кресло плетёное; обивка — ткань, цвет Tikkurila V451; Ш×Г×В 800×800×800 мм | | | аналог по характеристикам | шт. | 2 | | пом. 11; замена ≤ габарита |
| M_36 | Столик кофейный из тика; шпон, дуб натуральный, матовое масло; Ш×Г×В 1000×600×420 мм | | | аналог по характеристикам | шт. | 1 | | пом. 11; замена ≤ габарита |
| M_58 | Стул обеденный к столу M_32; обивка — ткань, цвет Tikkurila V451; каркас — дуб натуральный; Ш×Г×В 450×500×820 мм | | | аналог по характеристикам | шт. | 4 | | пом. 11; замена ≤ габарита |
| M_37 | Кровать 1800×2000, изголовье — мягкое в шерстяном твиде; обивка шерстяной твид, серо-коричневый, дерево — дуб массив, царги и ножки; Ш×Г×В 1800×2100×450 мм | | | аналог по характеристикам | шт. | 1 | | пом. 13; замена ≤ габарита |
| M_38, M_39 | Тумба прикроватная, массив ореха; дерево — орех массив, масло; Ш×Г×В 500×400×550 мм | | | аналог по характеристикам | шт. | 2 | | пом. 13; замена ≤ габарита |
| M_40 | Комод, дуб брашированный, фасады с кожаными ручками; дерево — дуб брашированный, масло; Ш×Г×В 1400×500×800 мм | | | аналог по характеристикам | шт. | 1 | | пом. 13; крепление к стене; замена ≤ габарита |
| M_41 | Кресло для чтения, букле (овечья шерсть); обивка букле, овечья шерсть, молочный; Ш×Г×В 800×800×900 мм | | | аналог по характеристикам | шт. | 1 | | пом. 13; замена ≤ габарита |
| M_42 | Ящики низкие под скатом (до колена 1200); шпон, дуб натуральный, матовое масло; Ш×Г×В 2600×500×1100 мм | | | аналог по характеристикам | шт. | 1 | | пом. 14; замена ≤ габарита |
| M_43 | Система хранения открытая в полную высоту (у перегородки, вне ската); каркас и полки — ЛДСП, декор «дуб натуральный»; Ш×Г×В 1400×500×2400 мм | | | аналог по характеристикам | шт. | 1 | | пом. 14; замена ≤ габарита |
| M_44 | Кровать 1600×2000, изголовье — вертикальная рейка из ясеня; дерево — ясень массив, рейка; Ш×Г×В 1600×2100×450 мм | | | аналог по характеристикам | шт. | 1 | | пом. 16; замена ≤ габарита |
| M_45 | Тумба подвесная, ясень; дерево — ясень шпон; Ш×Г×В 500×400×550 мм | | | аналог по характеристикам | шт. | 1 | | пом. 16; крепление к стене; замена ≤ габарита |
| M_47 | Дорожка беговая складная, полотно 1400×500; стальная рама, порошковая окраска, чёрный матовый; под тренажёр резиновый коврик 10 мм; Ш×Г×В 2000×800×1400 мм | | | аналог по характеристикам | шт. | 1 | | пом. 17; замена ≤ габарита |
| M_48 | Велотренажёр магнитный; стальная рама, порошковая окраска, чёрный матовый; под тренажёр — резиновый коврик 10 мм; Ш×Г×В 600×1100×1150 мм | | | аналог по характеристикам | шт. | 1 | | пом. 17; замена ≤ габарита |
| M_49 | Стеллаж низкий под скатом для книг и инвентаря; каркас и полки — ЛДСП, декор «дуб натуральный»; Ш×Г×В 2400×350×900 мм | | | аналог по характеристикам | шт. | 1 | | пом. 17; крепление к стене; замена ≤ габарита |
| M_50 | Стойка-этажерка для инвентаря: гантели 2–8 кг, эспандеры, ролик; стальная рама, порошковая окраска, чёрный матовый; гантели с обрезиненными дисками; Ш×Г×В 500×350×1000 мм | | | аналог по характеристикам | шт. | 1 | | пом. 17; крепление к стене; замена ≤ габарита |
| M_51 | Кровать 900×2000 с бортиком, массив сосны; дерево — сосна массив, воск; Ш×Г×В 900×2000×450 мм | | | аналог по характеристикам | шт. | 1 | | пом. 18; замена ≤ габарита |
| M_52 | Стол письменный, столешница ЛДСП светлый ясень, ножки — белая сталь; столешница ЛДСП «светлый ясень», ножки сталь, белая эмаль; Ш×Г×В 1200×600×750 мм | | | аналог по характеристикам | шт. | 1 | | пом. 18; замена ≤ габарита |
| M_54 | Кровать 900×2000 с ящиками, массив берёзы; дерево — берёза массив, масло; Ш×Г×В 900×2000×450 мм | | | аналог по характеристикам | шт. | 1 | | пом. 19; замена ≤ габарита |
| M_55 | Стол письменный растущий, берёзовая фанера на регулируемом каркасе; столешница — берёзовая фанера, лак; каркас сталь, тёмно-серая эмаль, регулировка 600–800; Ш×Г×В 1200×600×750 мм | | | аналог по характеристикам | шт. | 1 | | пом. 19; замена ≤ габарита |
| | **Техника встраиваемая и бытовая, светильники под розетки** | | | | | | | |
| | Посудомоечная машина встраиваемая, в модуле M_02; ниша 600 мм | | | аналог по характеристикам | шт. | 1 | | пом. 1; по схеме изготовителя |
| | Варочная панель встраиваемая, электрическая, в модуле M_04 | | | аналог по характеристикам | шт. | 1 | | пом. 1; по схеме изготовителя |

| | | | | | |
|---|---|---|---|---|---|
| | | | | | Проект: Дом 331 м² |
| | Лист | № док. | Подпись | Дата | Спецификация мебели и оборудования (продолжение) |
| Дизайнер | Кырлан А.С. | | | 19.10.26 | |

| Стадия | Лист | Листов |
|---|---|---|
| П | 16 | 156 |

Правка к этому листу

| Поз. | Наименование и техническая характеристика | Тип, марка, обозначение документа, опросного листа | Код продукции | Поставщик | Ед. измерения | Кол. | Масса 1 ед., кг | Примечание |
|---|---|---|---|---|---|---|---|---|
| | Духовой шкаф встраиваемый, в модуле M_04 | | | аналог по характеристикам | шт. | 1 | | пом. 1; по схеме изготовителя |
| | Холодильник встраиваемый, в модуле M_05 | | | аналог по характеристикам | шт. | 1 | | пом. 1; по схеме изготовителя |
| | Вытяжка встраиваемая, над модулем M_01 | | | аналог по характеристикам | шт. | 1 | | пом. 1; вывод P21 (ЭОМ) |
| | Стиральная машина | | | аналог по характеристикам | шт. | 1 | | пом. 3; вывод P7 (ЭОМ) |
| | Стиральная машина | | | аналог по характеристикам | шт. | 1 | | пом. 15; вывод P7 (ЭОМ) |
| | Стиральная машина, место по листу ВК (ОБ_02); Ш×Г 600×600 мм | | | аналог по характеристикам | шт. | 1 | | пом. 20; по схеме изготовителя |
| | Торшер; абажур — ткань или опаловое стекло; лампа 2700 K | | | аналог по характеристикам | шт. | 1 | | пом. 5; розетка P3 (ЭОМ) |
| | Торшер, у поз. M_40; абажур — ткань или опаловое стекло; лампа 2700 K | | | аналог по характеристикам | шт. | 1 | | пом. 13; розетка P5 (ЭОМ) |
| | **Текстиль** | | | | | | | |
| T14 | Рулонная штора кассетная, ткань димаут; полиэстер 100 %; цвет NCS S 2005-Y20R; карниз 890 мм, высота 2000 мм | | | аналог по характеристикам | шт. | 1 | | пом. 1 |
| T7 | Портьеры на люверсах, шерстяной твид; лён 100 %; цвет Farrow & Ball No. 40; карниз 1820 мм, высота 2760 мм, сборка 2 | | | аналог по характеристикам | шт. | 2 | | пом. 2 |
| T8 | Тюль, льняная сетка; полиэстер 100 %; цвет NCS S 0804-Y30R; карниз 1820 мм, высота 2760 мм, сборка 2,5 | | | аналог по характеристикам | шт. | 1 | | пом. 2 |
| T9 | Ковёр джутовый под диваном; шерсть 100 %; цвет Tikkurila X463; 1700×2300 мм | | | аналог по характеристикам | шт. | 1 | | пом. 2; с подложкой |
| T10 | Подушки на диван, кожа; букле (шерсть 60 %, полиэстер 40 %); цвет NCS S 3010-Y30R | | | аналог по характеристикам | шт. | 3 | | пом. 2 |
| T11 | Подушки на кровать, акцент; хлопковый бархат 100 %; цвет Farrow & Ball No. 298 | | | аналог по характеристикам | шт. | 2 | | пом. 2 |
| T12 | Плед на кровать; шерсть мериноса 100 %; цвет Farrow & Ball No. 298 | | | аналог по характеристикам | шт. | 1 | | пом. 2 |
| T1 | Портьеры-волна, два полотна; лён 100 %; цвет NCS S 2005-Y20R; карниз 2150 мм, высота 2760 мм, сборка 2 | | | аналог по характеристикам | шт. | 2 | | пом. 5 |
| T2 | Тюль-вуаль, одно полотно; полиэстер 100 %; цвет NCS S 0804-Y30R; карниз 2150 мм, высота 2760 мм, сборка 2,5 | | | аналог по характеристикам | шт. | 1 | | пом. 5 |
| T3 | Ковёр мягкой группы, шерсть с джутом; шерсть 100 %; цвет Farrow & Ball No. 243; 3600×2400 мм | | | аналог по характеристикам | шт. | 1 | | пом. 5; с подложкой |
| T4 | Подушки декоративные на диван, лён; лён 100 %; цвет Farrow & Ball No. 226 | | | аналог по характеристикам | шт. | 3 | | пом. 5 |
| T5 | Подушки декоративные на диван, акцент; хлопковый бархат 100 %; цвет Farrow & Ball No. 93 | | | аналог по характеристикам | шт. | 2 | | пом. 5 |
| T6 | Плед на диван; шерсть мериноса 100 %; цвет Farrow & Ball No. 93 | | | аналог по характеристикам | шт. | 1 | | пом. 5 |
| T40 | Покрытие резиновое модульное 500×500×10 мм под спортзону; резиновая крошка SBR с цветными EPDM-вкраплениями, плиты 500×500, 10 мм; цвет Farrow & Ball No. 243; 1500×6300 мм | | | аналог по характеристикам | шт. | 1 | | пом. 10 |
| T13 | Портьеры-волна, шерсть с блэкаут-подкладкой; лён 100 %; цвет Farrow & Ball No. 229; карниз 1800 мм, высота 2590 мм, сборка 2 | | | аналог по характеристикам | шт. | 2 | | пом. 13 |
| T15 | Тюль; полиэстер 100 %; цвет Little Greene No. 105; карниз 1800 мм, высота 2590 мм, сборка 2,5 | | | аналог по характеристикам | шт. | 1 | | пом. 13 |
| T16 | Ковёр под кроватью, шерсть ручного ткачества; шерсть 80 %, хлопок 20 %; цвет NCS S 2005-Y20R; 2800×1900 мм | | | аналог по характеристикам | шт. | 1 | | пом. 13; с подложкой |
| T17 | Подушки декоративные на кровать, шерсть-меланж; лён 100 %; цвет NCS S 2005-Y20R | | | аналог по характеристикам | шт. | 3 | | пом. 13 |
| T18 | Подушки на кровать, акцент; хлопковый бархат 100 %; цвет NCS S 7020-G10Y | | | аналог по характеристикам | шт. | 2 | | пом. 13 |
| T19 | Плед на кровать; шерсть мериноса 100 %; цвет NCS S 7020-G10Y | | | аналог по характеристикам | шт. | 1 | | пом. 13 |
| T20 | Портьеры-волна, хлопок-сатин с блэкаут-подкладкой; лён 100 %; цвет Tikkurila X463; карниз 1820 мм, высота 2610 мм, сборка 2 | | | аналог по характеристикам | шт. | 2 | | пом. 16 |
| T21 | Тюль, лён-вуаль; полиэстер 100 %; цвет Little Greene No. 105; карниз 1820 мм, высота 2610 мм, сборка 2,5 | | | аналог по характеристикам | шт. | 1 | | пом. 16 |
| T22 | Ковёр под кроватью, шерсть с узором ромбы; шерсть 100 %; цвет NCS S 3010-Y30R; 2000×2500 мм | | | аналог по характеристикам | шт. | 1 | | пом. 16; с подложкой |
| T23 | Подушки декоративные на кровать, хлопок-рогожка; букле (шерсть 60 %, полиэстер 40 %); цвет Tikkurila X463 | | | аналог по характеристикам | шт. | 3 | | пом. 16 |
| T24 | Подушки на кровать, акцент; хлопковый бархат 100 %; цвет Farrow & Ball No. 64 | | | аналог по характеристикам | шт. | 2 | | пом. 16 |
| T25 | Плед на кровать; шерсть мериноса 100 %; цвет Farrow & Ball No. 64 | | | аналог по характеристикам | шт. | 1 | | пом. 16 |
| T41 | Коврик для йоги и растяжки 1830×610×6, TPE, нескользящий; TPE, 6 мм, двухслойный; цвет NCS S 3020-G30Y; 610×1830 мм | | | аналог по характеристикам | шт. | 1 | | пом. 17 |
| T26 | Портьеры на люверсах, хлопок-канвас с блэкаут-подкладкой; лён 100 %; цвет Tikkurila V451; карниз 1820 мм, высота 2610 мм, сборка 2 | | | аналог по характеристикам | шт. | 2 | | пом. 18 |

| | | | | | |
|---|---|---|---|---|---|
| | Лист | № док. | Подпись | Дата | |
| Дизайнер | Кырлан А.С. | | | 19.10.26 | Проект: Дом 331 м² |
| | | | | | Спецификация мебели и оборудования (продолжение) |

| Стадия | Лист | Листов |
|---|---|---|
| П | 17 | 156 |

Правка к этому листу

| Поз. | Наименование и техническая характеристика | Тип, марка, обозначение документа, опросного листа | Код продукции | Поставщик | Ед. измерения | Кол. | Масса 1 ед., кг | Примечание |
|---|---|---|---|---|---|---|---|---|
| Т27 | Тюль, хлопковая кисея; полиэстер 100 %; цвет NCS S 0804-Y30R; карниз 1820 мм, высота 2610 мм, сборка 2,5 | | | аналог по характеристикам | шт. | 1 | | пом. 18 |
| Т28 | Ковёр под кроватью, хлопок, стираемый; шерсть 100 %; цвет NCS S 2005-Y20R; 1600×1200 мм | | | аналог по характеристикам | шт. | 1 | | пом. 18; с подложкой |
| Т29 | Подушки на кровать, хлопок-вельвет; букле (шерсть 60 %, полиэстер 40 %); цвет Tikkurila V451 | | | аналог по характеристикам | шт. | 3 | | пом. 18 |
| Т30 | Подушки на кровать, акцент; хлопковый бархат 100 %; цвет NCS S 3020-G30Y | | | аналог по характеристикам | шт. | 2 | | пом. 18 |
| Т31 | Плед на кровать; шерсть мериноса 100 %; цвет NCS S 3020-G30Y | | | аналог по характеристикам | шт. | 1 | | пом. 18 |
| Т32 | Портьеры-волна, лён-меланж с блэкаут-подкладкой; лён 100 %; цвет NCS S 2005-Y20R; карниз 1800 мм, высота 2590 мм, сборка 2 | | | аналог по характеристикам | шт. | 2 | | пом. 19 |
| Т33 | Тюль, лён-вуаль в мелкую клетку; полиэстер 100 %; цвет Farrow & Ball No. 226; карниз 1800 мм, высота 2590 мм, сборка 2,5 | | | аналог по характеристикам | шт. | 1 | | пом. 19 |
| Т34 | Ковёр под кроватью, шерсть с узором «горы»; шерсть 100 %; цвет NCS S 3010-Y30R; 1600×1200 мм | | | аналог по характеристикам | шт. | 1 | | пом. 19; с подложкой |
| Т35 | Подушки на кровать, хлопок-канвас с принтом; букле (шерсть 60 %, полиэстер 40 %); цвет Tikkurila X463 | | | аналог по характеристикам | шт. | 3 | | пом. 19 |
| Т36 | Подушки на кровать, акцент; хлопковый бархат 100 %; цвет NCS S 3040-Y70R | | | аналог по характеристикам | шт. | 2 | | пом. 19 |
| Т37 | Плед на кровать; шерсть мериноса 100 %; цвет NCS S 3040-Y70R | | | аналог по характеристикам | шт. | 1 | | пом. 19 |
| | **Декор** | | | | | | | |
| ДК8 | Часы настенные Ø400; 400×400 мм; центр на 1550 мм от пола | | | аналог по характеристикам | шт. | 1 | 2 | пом. 1; крепление: дюбель с крюком, 1 точка |
| ДК9 | Хлорофитум хохлатый на подоконнике (отм. +0,800); 300×200 мм; низ на 800 мм от пола | | | аналог по характеристикам | шт. | 1 | | пом. 1 |
| ДК23 | Ваза с тюльпанами на обеденном столе; 200×350 мм; на M_08 | | | аналог по характеристикам | шт. | 1 | | пом. 1 |
| ДК3 | Картина над диваном: офорт в паспарту, рама — орех; 1000×700 мм; низ на 1100 мм от пола | | | аналог по характеристикам | шт. | 1 | 4 | пом. 2; крепление к стене |
| ДК28 | Замиокулькас в кашпо Ø350; 350×350 мм | | | аналог по характеристикам | шт. | 1 | | пом. 2 |
| ДК1 | Картина над буфетом: пейзаж, масло, рама — морёный дуб; 1200×900 мм; низ на 1000 мм от пола | | | аналог по характеристикам | шт. | 1 | 6 | пом. 5; крепление: планка на дюбелях, 4 точки |
| ДК2 | Фикус лировидный в кашпо Ø400; 450×450 мм | | | аналог по характеристикам | шт. | 1 | | пом. 5 |
| ДК21 | Оливковое дерево в кашпо Ø450; 450×450 мм | | | аналог по характеристикам | шт. | 1 | | пом. 5 |
| ДК22 | Ваза с живыми цветами на журнальном столе; 200×350 мм; на M_19 | | | аналог по характеристикам | шт. | 1 | | пом. 5 |
| ДК5 | Зеркало; рама — чёрный матовый; 800×1800 мм; низ на 550 мм от пола | | | аналог по характеристикам | шт. | 1 | 18 | пом. 8; крепление: анкер, 4 шт. |
| ДК31 | Зеркало 1200×1500 для контроля техники, безопасное (плёнка), без рамы; 1200×1500 мм; низ на 600 мм от пола | | | аналог по характеристикам | шт. | 1 | 22 | пом. 10; крепление: анкер, 4 шт. |
| ДК24 | Гортензия крупнолистная в кадке Ø500; 500×500 мм | | | аналог по характеристикам | шт. | 1 | | пом. 11 |
| ДК25 | Самшит в кадке Ø450; 450×450 мм | | | аналог по характеристикам | шт. | 1 | | пом. 11 |
| ДК26 | Папоротник нефролепис в ящике 600×250; 250×600 мм | | | аналог по характеристикам | шт. | 1 | | пом. 11 |
| ДК4 | Картина над кроватью: акварель, рама — лиственница; 1000×700 мм; низ на 1300 мм от пола | | | аналог по характеристикам | шт. | 1 | 4 | пом. 13; крепление к стене |
| ДК27 | Фикус каучуконосный в кашпо Ø400; 400×400 мм | | | аналог по характеристикам | шт. | 1 | | пом. 13 |
| ДК6 | Картина над кроватью: натюрморт, масло, рама — тонкая латунь; 1000×700 мм; низ на 1300 мм от пола | | | аналог по характеристикам | шт. | 1 | 4 | пом. 16; крепление к стене |
| ДК7 | Зеркало в рост в раме из ясеня; рама — чёрный матовый; 600×1600 мм; низ на 300 мм от пола | | | аналог по характеристикам | шт. | 1 | 12 | пом. 16; крепление: анкер для пустотелых оснований, 4 шт. |
| ДК30 | Монстера в кашпо Ø450 с фитолампой; 450×450 мм | | | аналог по характеристикам | шт. | 1 | | пом. 17 |
| ДК10 | Картина над кроватью: детская иллюстрация, рама — светлый ясень; 600×700 мм; низ на 1100 мм от пола | | | аналог по характеристикам | шт. | 1 | 4 | пом. 18; крепление к стене |
| ДК11 | Зеркало безопасное (плёнка), рама — светлый ясень; рама — чёрный матовый; 500×1600 мм; низ на 300 мм от пола | | | аналог по характеристикам | шт. | 1 | 12 | пом. 18; крепление: анкер для пустотелых оснований, 4 шт. |
| ДК12 | Картина над кроватью: детский принт, рама — белёный дуб; 600×700 мм; низ на 1100 мм от пола | | | аналог по характеристикам | шт. | 1 | 4 | пом. 19; крепление к стене |
| ДК13 | Зеркало круглое Ø600 в кожаном ремне; рама — чёрный матовый; 600×600 мм; низ на 1150 мм от пола | | | аналог по характеристикам | шт. | 1 | 12 | пом. 19; крепление: анкер для пустотелых оснований, 4 шт. |

| | | | | | |
|---|---|---|---|---|---|
| | | | | | Проект: Дом 331 м² |
| | Лист | № док. | Подпись | Дата | Спецификация мебели и оборудования (продолжение) |
| Дизайнер | Кырлан А.С. | | | 19.10.26 | |

| Стадия | Лист | Листов |
|---|---|---|
| П | 18 | 156 |

Правка к этому листу

## Ведомость изделий

| Марка | Наименование | Пом. | Ш×Г×В, мм | Корпус | Фасад | Кромка, мм скр./вид. | Кол. |
|---|---|---|---|---|---|---|---|
| M_17 | Система хранения | 4 | 1200×400×2000 | ЛДСП 16 | без фасадов; ящики — МДФ 18, эмаль матовая | 0,4 / 2 | 1 |
| M_23 | Система хранения | 7 | 2600×500×2200 | ЛДСП 16 | без фасадов; ящики — МДФ 18, эмаль матовая | 0,4 / 2 | 1 |
| M_24 | Шкаф-купе | 8 | 1400×600×2600 | ЛДСП 16 | рифлёные панели МДФ в алюминиевом профиле | 0,4 / 2 | 1 |
| M_26 | Система хранения | 10 | 3000×500×2000 | ЛДСП 16 | без фасадов; ящики — МДФ 18, эмаль матовая | 0,4 / 2 | 1 |
| M_43 | Система хранения | 14 | 1400×500×2400 | ЛДСП 16 | без фасадов; ящики — МДФ 18, эмаль матовая | 0,4 / 2 | 1 |
| M_46 | Шкаф распашной | 16 | 2000×600×2400 | ЛДСП 16 | МДФ 18, эмаль матовая | 0,4 / 2 | 1 |
| M_49 | Система хранения | 17 | 2400×350×900 | ЛДСП 16 | без фасадов; ящики — МДФ 18, эмаль матовая | 0,4 / 2 | 1 |
| M_53 | Шкаф распашной | 18 | 1000×600×2200 | ЛДСП 16 | МДФ 18, эмаль матовая | 0,4 / 2 | 1 |
| M_56 | Шкаф распашной | 19 | 1000×600×2200 | ЛДСП 16 | МДФ 18, эмаль матовая | 0,4 / 2 | 1 |
| M_06 | Модуль нижний: ящики | 1 | 800×600×900 | ЛДСП 16 | МДФ 18, эмаль матовая | 0,4 / 2 | 1 |
| M_11 | Модуль навесной: полки | 1 | 500×350×900 | ЛДСП 16 | МДФ 18, эмаль матовая | 0,4 / 2 | 1 |
| M_01 | Модуль нижний: мойка | 1 | 800×600×900 | ЛДСП 16 | МДФ 18, эмаль матовая | 0,4 / 2 | 1 |
| M_02 | Модуль нижний: ПММ | 1 | 600×600×900 | ЛДСП 16 | МДФ 18, эмаль матовая | 0,4 / 2 | 1 |
| M_09 | Модуль навесной: полки | 1 | 600×350×900 | ЛДСП 16 | МДФ 18, эмаль матовая | 0,4 / 2 | 1 |
| M_03 | Модуль нижний: ящики | 1 | 400×600×900 | ЛДСП 16 | МДФ 18, эмаль матовая | 0,4 / 2 | 1 |
| M_04 | Модуль нижний: духовой шкаф, варочная | 1 | 800×600×900 | ЛДСП 16 | МДФ 18, эмаль матовая | 0,4 / 2 | 1 |
| M_10 | Модуль навесной: полки | 1 | 400×350×900 | ЛДСП 16 | МДФ 18, эмаль матовая | 0,4 / 2 | 1 |
| M_05 | Пенал: холодильник встр. | 1 | 700×650×2200 | ЛДСП 16 | МДФ 18, эмаль матовая | 0,4 / 2 | 1 |
| M_12 | Пенал: полки | 1 | 600×600×2200 | ЛДСП 16 | МДФ 18, эмаль матовая | 0,4 / 2 | 1 |

## Ведомость встраиваемой техники

| Поз. | Прибор | Ниша, вырез, мм | Вентиляция | Питание | Схема |
|---|---|---|---|---|---|
| M_01 | Мойка врезная / подстольная с сифоном | вырез по шаблону, ориентир 700 × 480 | | смеситель — выводы ВК | по модели |
| M_02 | Посудомоечная машина встраиваемая, 60 см | ниша 600 × 862 (от пола до низа столешницы) | зазор в цоколе, по схеме | розетка в соседнем модуле | по модели |
| M_04 | Духовой шкаф встраиваемый, 60 см | ниша 560 × 595, глубина ≥ 550 | зазор за шкафом, вырез в задней стенке | вывод кабеля под шкафом | по модели |
| M_04 | Варочная панель индукционная, 60 см | вырез в столешнице 560 × 490 | | вывод кабеля под модулем | по модели |
| M_05 | Холодильник встраиваемый, ниша 1780 | ниша 1780 × 560 × 550 | решётка в цоколе, канал за корпусом, выход сверху | розетка над нишей или в соседнем модуле | по модели |
| M_04 | Вытяжка настенная, 60 см | низ ≥ 650 над панелью | воздуховод к вентканалу, короб до потолка | вывод кабеля в коробе | по модели |

## Ведомость фурнитуры

| № | Фурнитура | Тип, размер | Изделия | Кол. |
|---|---|---|---|---|
| 1 | Штанга выдвижная торцевая | L по глубине | M_17, M_23, M_26, M_43, M_49 | 9 |
| 2 | Полкодержатель с фиксацией | ø5 мм | M_17, M_23, M_24, M_26, M_43, M_46, M_49, M_53, M_56, M_11, M_09, M_10, M_05, M_12 | 220 |
| 3 | Опора регулируемая с цоколем на клипсах | ход 20 мм | M_17, M_23, M_24, M_26, M_43, M_46, M_49, M_53, M_56 | 66 |
| 4 | Анкер по основанию стены | по таблице крепежа | M_17, M_23, M_24, M_26, M_43, M_46, M_49, M_53, M_56, M_11, M_09, M_10 | 75 |
| 5 | Уголок крепления к стене от опрокидывания | стальной | M_17, M_23, M_24, M_26, M_43, M_46, M_49, M_53, M_56, M_05, M_12 | 22 |
| 6 | Система дверей купе: профиль, направляющие, ролики | на 2 двери | M_24 | 1 |
| 7 | Ручка-профиль вертикальная | в цвет профиля | M_24 | 2 |
| 8 | Штанга овальная 30×15, L = 676 | + 2 держателя | M_24 | 1 |
| 9 | Полка для обуви выдвижная наклонная | ширина 676 | M_24 | 3 |
| 10 | Петля накладная 110° с доводчиком | чашка 35 мм | M_46, M_53, M_56, M_11, M_01, M_09, M_10, M_05, M_12 | 72 |
| 11 | Штанга овальная 30×15, L = 976 | + 2 держателя | M_46 | 1 |
| 12 | Штанга овальная 30×15, L = 968 | + 2 держателя | M_53, M_56 | 2 |
| 13 | Направляющие полного выдвижения с доводчиком NL 500 | пара | M_06, M_03, M_04 | 7 |
| 14 | Ручка-профиль | латунь матовая | M_06, M_11, M_01, M_02, M_09, M_03, M_04, M_10, M_05, M_12 | 19 |
| 15 | Опора кухонная регулируемая 100–120 мм | + клипса цоколя | M_06, M_01, M_02, M_03, M_04, M_05, M_12 | 36 |
| 16 | Навес регулируемый для навесного шкафа | пара на секцию | M_11, M_09, M_10 | 3 |
| 17 | Шина монтажная | L = 440 | M_11 | 1 |
| 18 | Комплект навески фасада ПММ | из поставки машины | M_02 | 1 |
| 19 | Шина монтажная | L = 540 | M_09 | 1 |
| 20 | Шина монтажная | L = 340 | M_10 | 1 |

## Примечания

1. Модели техники выбирает заказчик до изготовления мебели; ниши, вырезы и вентиляция — по монтажной схеме выбранной модели (условие гарантии), её номер вносится в ведомость.
2. Количество фурнитуры — по чертежам изделий; запас крепежа 5 %. Аналоги — по характеристикам (доводчик, нагрузка, ход).
3. Цвет корпусов, фасадов и профилей — по колерной карте проекта.

| | | | | | |
|---|---|---|---|---|---|
| | | | | | Проект: Дом 331 м² |
| | Лист | № док. | Подпись | Дата | Ведомости изделий, техники и фурнитуры |
| Дизайнер | Кырлан А.С. | | | 19.10.26 | |

| Стадия | Лист | Листов |
|---|---|---|
| П | 19 | 156 |

выпуск 18.10.2026 № 8cd922c868 · стр. 19 из 156

Правка к этому листу

## Фрагмент 1. Санузел 1 этажа (пом. 3)

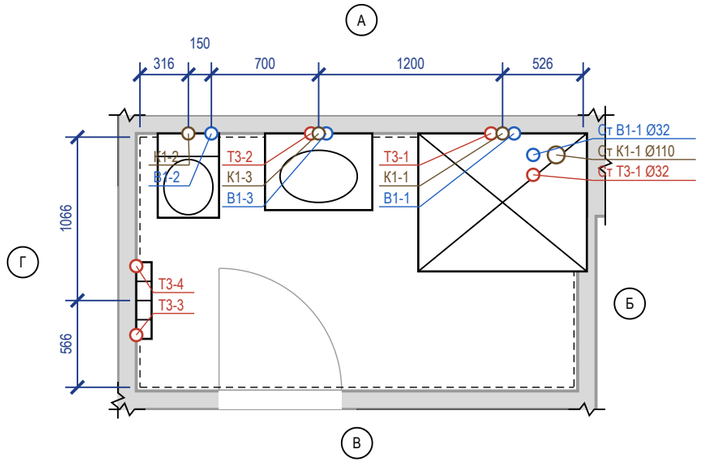


## Фрагмент 2. Кухня-столовая (пом. 1)

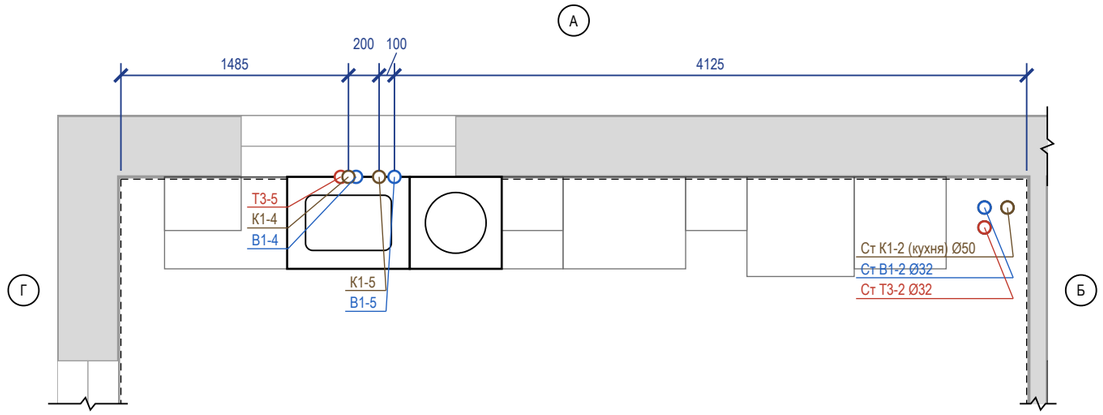


## Ведомость привязок выводов

| Код | Прибор | Ø | H, мм | Привязка от чист. стен, мм | Прим. |
|---|---|---|---|---|---|
| В1-1 | С_01 душ | ½" | 1200 | ст. А: 451 от Б | межос. 150 |
| Т3-1 | С_01 душ | ½" | 1200 | ст. А: 601 от Б | межос. 150 |
| К1-1 | С_01 душ | Ø50 | 70 | ст. А: 526 от Б | сифон поддона |
| В1-2 | С_02 унитаз подвесной | ½" | 250 | ст. А: 466 от Г | в раме инсталляции |
| К1-2 | С_02 унитаз подвесной | Ø110 | 220 | ст. А: 316 от Г | |
| В1-3 | С_03 умывальник | ½" | 600 | ст. А: 1216 от Г | межос. 100 |
| Т3-2 | С_03 умывальник | ½" | 600 | ст. А: 1116 от Г | межос. 100 |
| К1-3 | С_03 умывальник | Ø50 | 500 | ст. А: 1166 от Г | |
| Т3-3 | С_04 полотенцесушитель | ½" | 1150 | ст. Г: 341 от В | подача, межос. 450; байпас и краны |
| Т3-4 | С_04 полотенцесушитель | ½" | 1150 | ст. Г: 791 от В | обратка |
| В1-4 | П5 мойка кухонная | ½" | 600 | ст. А: 1535 от Г | межос. 100 |
| Т3-5 | П5 мойка кухонная | ½" | 600 | ст. А: 1435 от Г | межос. 100 |
| К1-4 | П5 мойка кухонная | Ø50 | 400 | ст. А: 1485 от Г | |
| В1-5 | П6 посудомоечная машина | ½" | 550 | ст. А: 1785 от Г | кран ПММ в шкафу мойки |
| К1-5 | П6 посудомоечная машина | Ø40 | 550 | ст. А: 1685 от Г | слив ПММ в шкафу мойки |

## Условные обозначения

- вывод В1 (код — в ведомости привязок)
- вывод Т3 (код — в ведомости привязок)
- вывод К1 (код — в ведомости привязок)
- сантехприбор по расстановке (габарит модели)
- чистовая поверхность стены (от неё привязки)
- стояк «Ст К1-N / Ст В1-N» (ГОСТ 21.601), Ø мм
- линия обрыва (граница фрагмента)
- А — обозначение стены А–Г (как на развёртках)

## Примечания

1. Привязки выводов даны от чистовых поверхностей стен (облицовка на сторону: санузел 1 этажа — 24 мм (штукатурка 10 + клей 5 + плитка 9); кухня-столовая — 22 мм (фартук: штукатурка 10 + клей 3 + плитка 9)); эти же грани — на развёртках и в раскладке плитки. Высоты — от чистого пола помещения.
2. До черновой разводки сверить по паспорту выбранного прибора (смеситель, инсталляция, сифон).
3. Горячая вода (Т3) — слева от холодной (В1), если смотреть на прибор. Допуск установки выводов: ±5 мм в группе, ±20 мм у отдельно стоящих.
4. Расчёт систем водоснабжения и канализации и подбор оборудования выполняет проектная организация; лист задаёт места и высоты выводов.
5. Посудомоечная машина П6: кран и слив — отдельными выводами в шкафу мойки (не за машиной), до машины ≤ 1500 мм.
6. Прибор П5 мойка кухонная, П6 посудомоечная машина взят из расстановки мебели (по шкафу с мойкой).
7. Стояки в коробах/шахтах не замоноличивать; стояк К1 в коробе — звукоизоляция стояка в коробе без жёсткого контакта с трубой; к арматуре и ревизиям — люк не меньше 300×400.

| | | | | | |
|---|---|---|---|---|---|
| | | | | | Проект: Дом 331 м² |
| | Лист | № док. | Подпись | Дата | План выводов сантехники · 1-й этаж |
| Дизайнер | Кырлан А.С. | | | 19.10.26 | Стадия: П; Лист: 20; Листов: 156 |

Правка к этому листу

## Фрагмент 1. Санузел мастер (пом. 15)

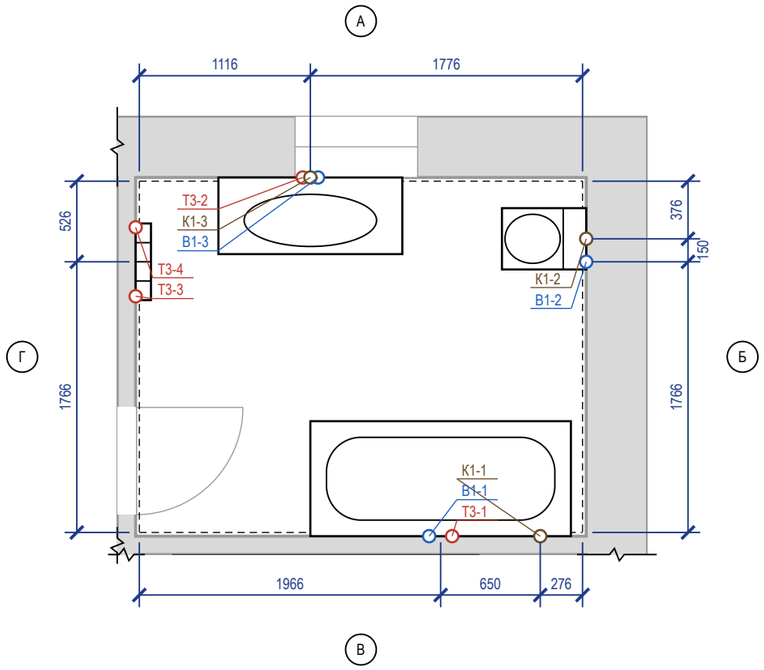


## Фрагмент 2. Санузел 2 (пом. 20)

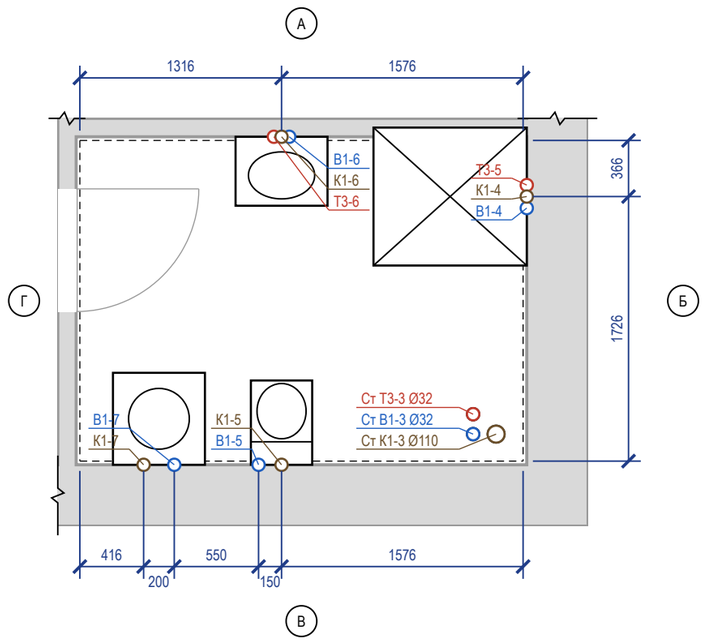


## Ведомость привязок выводов

| Код | Прибор | Ø | H, мм | Привязка от чист. стен, мм | Прим. |
|---|---|---|---|---|---|
| В1-1 | С_05 ванна | ½" | 800 | ст. В: 1001 от Б | межос. 150 |
| Т3-1 | С_05 ванна | ½" | 800 | ст. В: 851 от Б | межос. 150 |
| К1-1 | С_05 ванна | Ø50 | 50 | ст. В: 276 от Б | |
| В1-2 | С_06 унитаз подвесной | ½" | 250 | ст. Б: 526 от А | в раме инсталляции |
| К1-2 | С_06 унитаз подвесной | Ø110 | 220 | ст. Б: 376 от А | |
| В1-3 | С_07 умывальник | ½" | 600 | ст. А: 1166 от Г | межос. 100 |
| Т3-2 | С_07 умывальник | ½" | 600 | ст. А: 1066 от Г | межос. 100 |
| К1-3 | С_07 умывальник | Ø50 | 500 | ст. А: 1116 от Г | |
| Т3-3 | С_08 полотенцесушитель | ½" | 1150 | ст. Г: 751 от А | подача, межос. 450; байпас и краны |
| Т3-4 | С_08 полотенцесушитель | ½" | 1150 | ст. Г: 301 от А | обратка |
| В1-4 | С_09 душ | ½" | 1200 | ст. Б: 441 от А | межос. 150 |
| Т3-5 | С_09 душ | ½" | 1200 | ст. Б: 291 от А | межос. 150 |
| К1-4 | С_09 душ | Ø50 | 70 | ст. Б: 366 от А | сифон поддона |
| В1-5 | С_10 унитаз подвесной | ½" | 250 | ст. В: 1166 от Г | в раме инсталляции |
| К1-5 | С_10 унитаз подвесной | Ø110 | 220 | ст. В: 1316 от Г | |
| В1-6 | С_11 умывальник | ½" | 600 | ст. А: 1366 от Г | межос. 100 |
| Т3-6 | С_11 умывальник | ½" | 600 | ст. А: 1266 от Г | межос. 100 |
| К1-6 | С_11 умывальник | Ø50 | 500 | ст. А: 1316 от Г | |
| В1-7 | ОБ_02 стиральная машина | ½" | 600 | ст. В: 616 от Г | кран машины |
| К1-7 | ОБ_02 стиральная машина | Ø50 | 600 | ст. В: 416 от Г | |

## Условные обозначения

- вывод В1 (код — в ведомости привязок)
- вывод Т3 (код — в ведомости привязок)
- вывод К1 (код — в ведомости привязок)
- сантехприбор по расстановке (габарит модели)
- чистовая поверхность стены (от неё привязки)
- стояк «Ст К1-N / Ст В1-N» (ГОСТ 21.601), Ø мм
- линия обрыва (граница фрагмента)
- А — обозначение стены А–Г (как на развёртках)

## Примечания

1. Привязки выводов даны от чистовых поверхностей стен (облицовка на сторону: санузел мастер — 24 мм (штукатурка 10 + клей 5 + плитка 9); санузел 2 24 мм (штукатурка 10 + клей 5 + плитка 9)); эти же грани — на развёртках и в раскладке плитки. Высоты — от чистого пола помещения.
2. До черновой разводки сверить по паспорту выбранного прибора (смеситель, инсталляция, сифон).
3. Горячая вода (Т3) — слева от холодной (В1), если смотреть на прибор. Допуск установки выводов: ±5 мм в группе, ±20 мм у отдельно стоящих.
4. Расчёт систем водоснабжения и канализации и подбор оборудования выполняет проектная организация; лист задаёт места и высоты выводов.
5. Стояки в коробах/шахтах не замоноличивать; стояк К1 в коробе — звукоизоляция стояка в коробе без жёсткого контакта с трубой; к арматуре и ревизиям — люк не меньше 300×400.

| | | | | | |
|---|---|---|---|---|---|
| | | | | | Проект: Дом 331 м² |
| | Лист | № док. | Подпись | Дата | План выводов сантехники · Мансарда |
| Дизайнер | Кырлан А.С. | | | 19.10.26 | |

| Стадия | Лист | Листов |
|---|---|---|
| П | 21 | 156 |

Правка к этому листу

## План квартиры (М 1:400)

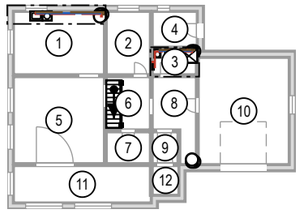


## Фр. 1. Санузел 1 этажа (М 1:25)

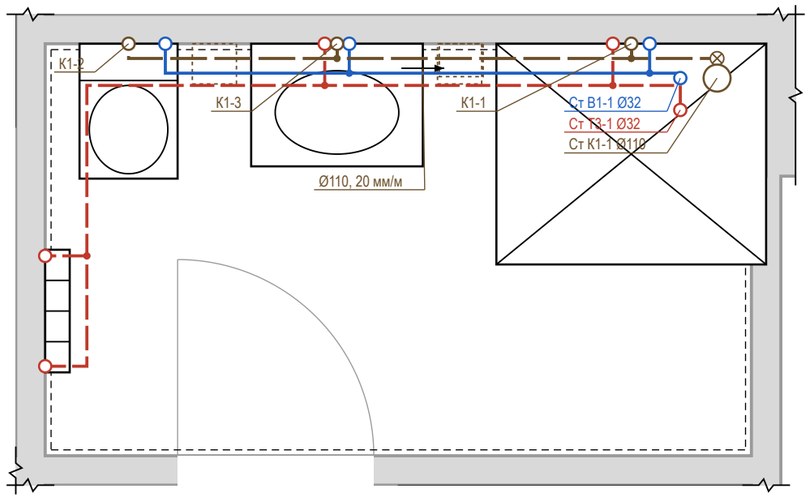


## Фр. 2. Кухня-столовая (М 1:25)

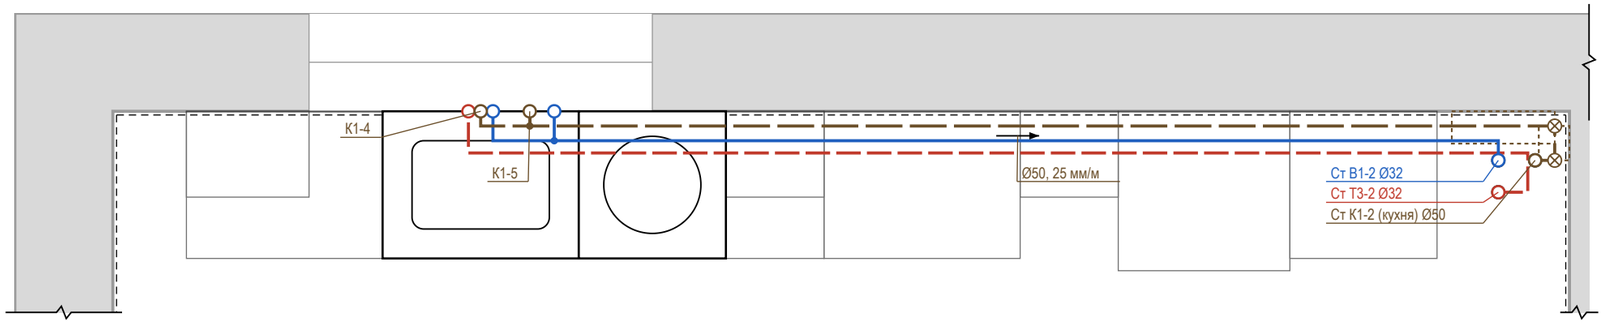


## Условные обозначения

- В1 — водопровод хозяйственно-питьевой (ХВС), PP-R Ø20
- Т3 — горячее водоснабжение, подача (ГВС), PP-R Ø20
- К1 — канализация бытовая
- направление уклона К1 / пола: Ø, мм на 1 м
- ревизия (прочистка) К1 — доступ сохранить
- тройник (ответвление к прибору)
- короб К1 над чистым полом (ГКЛВ под плитку)
- вывод В1 (код — в ведомости привязок)
- вывод Т3 (код — в ведомости привязок)
- вывод К1 (код — в ведомости привязок)
- сантехприбор по расстановке (габарит модели)
- стояк «Ст К1-N / Ст В1-N» (ГОСТ 21.601), Ø мм
- линия обрыва (граница фрагмента)
- граница фрагмента на плане (Фр. N)

## Профиль выпусков К1 (до врезки в стояк)

| Выпуск | Прибор | Ø | L, м | i, мм/м | Δh, мм | Прокладка, мм |
|---|---|---|---|---|---|---|
| К1-2 | С_02 унитаз подвесной | Ø110 | 2,54 | 20 | 51 | короб 200×140 |
| К1-4 | П5 мойка кухонная | Ø50 | 4,66 | 25 | 117 | короб 200×110 |
| К1-3 | С_03 умывальник | Ø50 | 1,69 | 25 | 42 | короб 130×110 |
| К1-1 | С_01 душ | Ø50 | 0,49 | 25 | 12 | над полом за приборами |
| К1-5 | П6 посудомоечная машина | Ø40 | 4,46 | 30 | 134 | короб 210×110 |

Короб h×b: h — от чистого пола, b — от чистовой стены. Стяжка 35 мм — лист полов.

## Узел ввода В1, Т3 (схема, без масштаба)

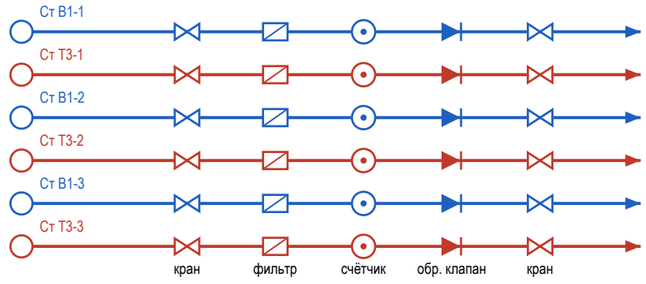


⊗ Ст К1-1, Ст К1-2 (кухня), Ст К1-3: ревизия на стояке — люк в коробе

## Примечания

1. Трассы принципиальные, построены от стояков вдоль стен помещений; фактическое положение фиксируется исполнительной схемой с привязками (фото с рулеткой) до закрытия.
2. Уклон К1 не менее 1/d и не более 150 мм/м (СП 30.13330.2020, п. 19.1), приняты практические уклоны; поворот — двумя отводами 45°, ревизия после поворота, доступ сохранить. Стояк К1 в коробе — звукоизоляция стояка в коробе, без жёсткого контакта короба с трубой.
3. Решение по К1: стяжка 35 мм не укрывает трубы (нужно Ø + Δh + 45 мм) — выпуски идут над чистым полом вдоль стен: К1-1 — за приборами и в раме инсталляции; К1-2, К1-4, К1-3, К1-5 — в коробе ГКЛВ под плитку (размеры в профиле). Короба — на развёртках; отметку низа врезки в стояк замерить до черновых работ.
4. На каждом вводе В1 и Т3 — кран шаровой, фильтр, счётчик, обратный клапан; доступ через люк не меньше 300×400. Водопровод — в штробе стен или в коробах; трубы испытать давлением до закрытия (акт скрытых работ).
5. Расчёт систем, диаметры магистралей и подбор оборудования выполняет проектная организация; врезка и перенос стояков — по согласованию с управляющей организацией. Арматуру и привязки сверить по паспортам приборов.

| | | | | | |
|---|---|---|---|---|---|
| | | | | | Проект: Дом 331 м² |
| | Лист | № док. | Подпись | Дата | Схема разводки водопровода и канализации · 1-й этаж |
| Дизайнер | Кырлан А.С. | | | 19.10.26 | |

| Стадия | Лист | Листов |
|---|---|---|
| П | 22 | 156 |

## План квартиры (М 1:200)

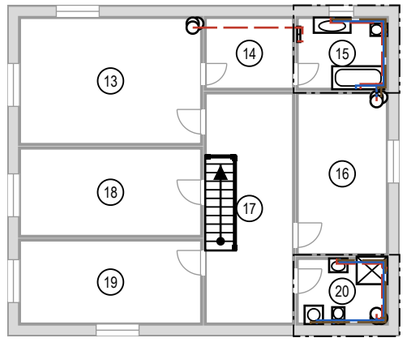


## Фр. 1. Санузел мастер (М 1:40)

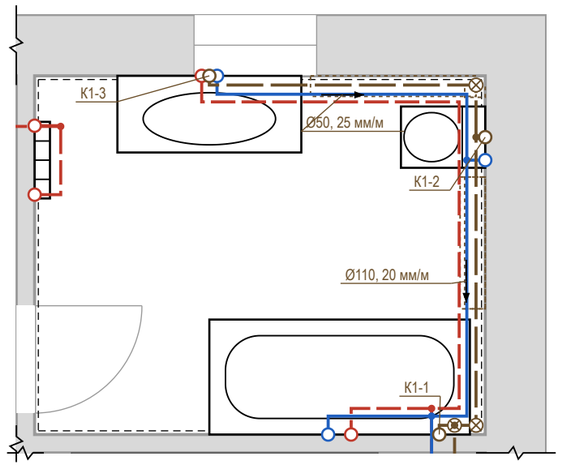


## Фр. 2. Санузел 2 (М 1:40)

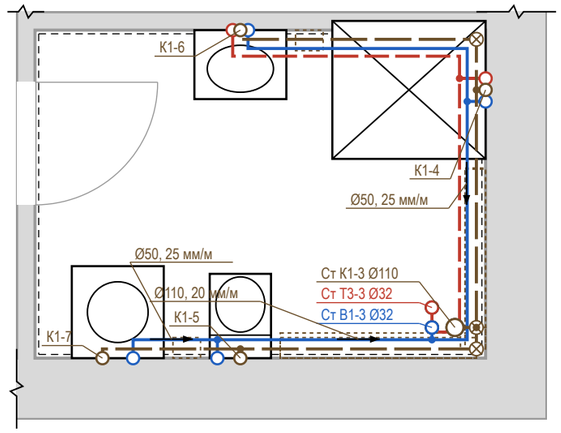


## Условные обозначения

- В1 — водопровод хозяйственно-питьевой (ХВС), PP-R Ø20
- Т3 — горячее водоснабжение, подача (ГВС), PP-R Ø20
- К1 — канализация бытовая
- направление уклона К1 / пола: Ø, мм на 1 м
- ⊗ ревизия (прочистка) К1 — доступ сохранить
- • тройник (ответвление к прибору)
- ▭ короб К1 над чистым полом (ГКЛВ под плитку)
- ○ вывод В1 (код — в ведомости привязок)
- ○ вывод Т3 (код — в ведомости привязок)
- ○ вывод К1 (код — в ведомости привязок)
- ▭ сантехприбор по расстановке (габарит модели)
- ◯ стояк «Ст К1-N / Ст В1-N» (ГОСТ 21.601), Ø мм
- ∿ линия обрыва (граница фрагмента)
- ▭ граница фрагмента на плане (Фр. N)

## Профиль выпусков К1 (до врезки в стояк)

| Выпуск | Прибор | Ø | L, м | i, мм/м | Δh, мм | Прокладка, мм |
|---|---|---|---|---|---|---|
| К1-2 | С_06 унитаз подвесной | Ø110 | 2,40 | 20 | 48 | короб 190×140 |
| К1-5 | С_10 унитаз подвесной | Ø110 | 1,88 | 20 | 38 | короб 180×140 |
| К1-3 | С_07 умывальник | Ø50 | 4,48 | 25 | 112 | короб 200×110 |
| К1-6 | С_11 умывальник | Ø50 | 3,62 | 25 | 91 | короб 180×110 |
| К1-7 | ОБ_02 стиральная машина | Ø50 | 2,78 | 25 | 70 | короб 150×110 |
| К1-4 | С_09 душ | Ø50 | 1,75 | 25 | 44 | короб 130×110 |
| К1-1 | С_05 ванна | Ø50 | 0,48 | 25 | 12 | над полом за приборами |

Короб h×b: h — от чистого пола, b — от чистовой стены. Стяжка 35 мм — лист полов.

## Узел ввода В1, Т3 (схема, без масштаба)

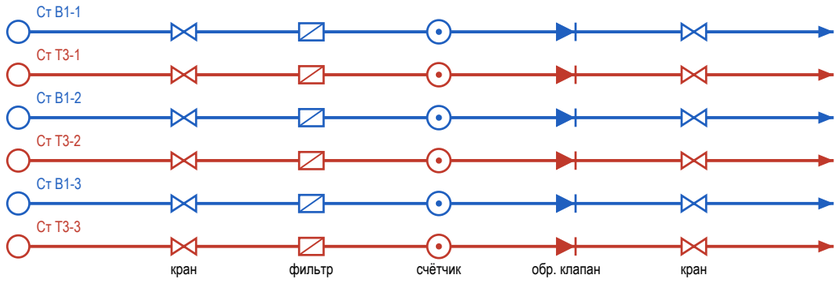


⊗ Ст К1-1, Ст К1-2 (кухня), Ст К1-3: ревизия на стояке — люк в коробе

## Примечания

1. Трассы принципиальные, построены от стояков вдоль стен помещений; фактическое положение фиксируется исполнительной схемой с привязками (фото с рулеткой) до закрытия.
2. Уклон К1 не менее 1/d и не более 150 мм/м (СП 30.13330.2020, п. 19.1), приняты практические уклоны; поворот — двумя отводами 45°, ревизия после поворота, доступ сохранить. Стояк К1 в коробе — звукоизоляция стояка в коробе, без жёсткого контакта короба с трубой.
3. Решение по К1: стяжка 35 мм не укрывает трубы (нужно Ø + Δh + 45 мм) — выпуски идут над чистым полом вдоль стен: К1-1 — за приборами и в раме инсталляции; К1-2, К1-5, К1-3, К1-6, К1-7, К1-4 — в коробе ГКЛВ под плитку (размеры в профиле). Короба — на развёртках; отметку низа врезки в стояк замерить до черновых работ.
4. На каждом вводе В1 и Т3 — кран шаровой, фильтр, счётчик, обратный клапан; доступ через люк не меньше 300×400. Водопровод — в штробе стен или в коробах; трубы испытать давлением до закрытия (акт скрытых работ).
5. Расчёт систем, диаметры магистралей и подбор оборудования выполняет проектная организация; врезка и перенос стояков — по согласованию с управляющей организацией. Арматуру и привязки сверить по паспортам приборов.

| | | | | | |
|---|---|---|---|---|---|
| | | | | | Проект: Дом 331 м² |
| | Лист | № док. | Подпись | Дата | Схема разводки водопровода и канализации · Мансарда |
| Дизайнер | Кырлан А.С. | | | 19.10.26 | |

| Стадия | Лист | Листов |
|---|---|---|
| П | 23 | 156 |

выпуск 18.10.2026 № 8cd922c868 · стр. 23 из 156

Правка к этому листу

| Поз. | Наименование и техническая характеристика | Тип, марка, обозначение документа | Код продукции | Поставщик | Ед. изм. | Кол. | Масса 1 ед., кг | Примечание |
|---|---|---|---|---|---|---|---|---|
| | Санитарные приборы | | | | | | | |
| 1 | Ванна акриловая 1700×750 мм, с каркасом, экраном и отверстием слив-перелив | аналог | | выбор заказчика | шт | 1 | | С_05 |
| 2 | Унитаз подвесной безободковый, с сиденьем микролифт, крепёж и звукоизолирующая прокладка | Jacob Delafon Struktura EDF102-00 | | выбор заказчика | шт | 3 | | С_02, С_06, С_10 |
| 3 | Инсталляция для подвесного унитаза: рама высотой 1120 мм, бачок, клавиша смыва (ось клавиши 1050 мм от чистого пола) | аналог | | выбор заказчика | шт | 3 | | С_02, С_06, С_10; короб ГКЛВ |
| 4 | Умывальник подвесной 700×500 мм, с отверстием под смеситель и переливом | аналог | | выбор заказчика | шт | 1 | | С_03 |
| 5 | Умывальник подвесной 1200×500 мм, с отверстием под смеситель и переливом | аналог | | выбор заказчика | шт | 1 | | С_07 |
| 6 | Умывальник подвесной 600×450 мм, с отверстием под смеситель и переливом | аналог | | выбор заказчика | шт | 1 | | С_11 |
| 7 | Поддон душевой низкий 1100×900 мм, с сифоном и выпуском Ø50, на ножках/подиуме | аналог | | выбор заказчика | шт | 1 | | С_01 |
| 8 | Поддон душевой низкий 900×1000 мм, с сифоном и выпуском Ø50, на ножках/подиуме | аналог | | выбор заказчика | шт | 1 | | С_09 |
| 9 | Мойка кухонная 800×600 мм, с переливом | аналог | | с кухонной мебелью | шт | 1 | | П13 |
| 10 | Полотенцесушитель водяной (ГВС), с байпасом и кранами | аналог | | выбор заказчика | шт | 2 | | С_04, С_08 |
| | Смесители, сифоны и арматура приборов | | | | | | | |
| 11 | Смеситель для ванны настенный однорычажный, межосевое 150 мм, с душевым набором (лейка, шланг, держатель) | аналог | | выбор заказчика | шт | 1 | | С_05 |
| 12 | Смеситель для умывальника однорычажный, с донным клапаном | аналог | | выбор заказчика | шт | 3 | | С_03, С_07, С_11 |
| 13 | Душевая система скрытого монтажа с термостатом: встраиваемая часть, верхний душ, ручная лейка | аналог | | выбор заказчика | шт | 2 | | С_01, С_09; встраиваемая часть — до плитки |
| 14 | Смеситель кухонный однорычажный, высокий излив | аналог | | выбор заказчика | шт | 1 | | П13 |
| 15 | Обвязка ванны слив-перелив Ø40/50 с сифоном | аналог | | выбор заказчика | шт | 1 | | С_05 |
| 16 | Сифон для умывальника бутылочный Ø32/40–50, с гофрой к выпуску | аналог | | выбор заказчика | шт | 3 | | С_03, С_07, С_11 |
| 17 | Сифон для мойки с отводом для ПММ Ø40/50 | аналог | | выбор заказчика | шт | 1 | | П13 |
| 18 | Сифон для стиральной машины встраиваемый в стену Ø50, с обратным клапаном | аналог | | выбор заказчика | шт | 1 | | ОБ_02 |
| 19 | Кран угловой ½"×½" с гибкой подводкой 40 см (умывальники, мойка) | аналог | | выбор заказчика | шт | 8 | | по 2 на прибор |
| 20 | Кран шаровой угловой ½"×¾" для подключения стиральной и посудомоечной машины | аналог | | выбор заказчика | шт | 2 | | ОБ_02, П14 |
| 21 | Узел подключения полотенцесушителя: байпас Ду20, краны шаровые ½" ×2 | аналог | | выбор заказчика | шт | 2 | | |
| | Трубопроводы | | | | | | | |
| 22 | Труба полипропиленовая PP-R PN20 Ø20×3,4 (В1) | ГОСТ 32415-2013 | | выбор заказчика | м | 28,5 | 0,17 | 18,3 + 7,5 + 10 % |
| 23 | Труба PP-R, армированная стекловолокном, PN20 Ø20×2,8 (Т3) | ГОСТ 32415-2013 | | выбор заказчика | м | 36 | 0,15 | 22,5 + 10,2 + 10 % |
| 24 | Труба канализационная ПП Ø40 (К1) | ГОСТ 32414-2013 | | выбор заказчика | м | 1 | | 0,1 + 0,6 + 10 % |
| 25 | Труба канализационная ПП Ø50 (К1) | ГОСТ 32414-2013 | | выбор заказчика | м | 16 | | 11,6 + 2,7 + 10 % |
| 26 | Труба канализационная ПП Ø110 (К1) | ГОСТ 32414-2013 | | выбор заказчика | м | 8,5 | | 6,7 + 0,7 + 10 % |
| | Фасонные части и выводы | | | | | | | |
| 27 | Отвод канализационный ПП 45° Ø50 | ГОСТ 32414-2013 | | выбор заказчика | шт | 18 | | 2 шт. на поворот |
| 28 | Отвод канализационный ПП 45° Ø110 | ГОСТ 32414-2013 | | выбор заказчика | шт | 16 | | 2 шт. на поворот |
| 29 | Тройник канализационный ПП 45° (врезки ветвей) | ГОСТ 32414-2013 | | выбор заказчика | шт | 11 | | |
| 30 | Ревизия канализационная ПП (после поворота трассы) | ГОСТ 32414-2013 | | выбор заказчика | шт | 9 | | доступ сохранить |
| 31 | Фитинги PP-R Ø20: тройники, угольники 90° (ветви и повороты В1, Т3) | ГОСТ 32415-2013 | | выбор заказчика | шт | 51 | | |
| 32 | Водорозетка PP-R Ø20×½" настенная, с креплением | ГОСТ 32415-2013 | | выбор заказчика | шт | 23 | | коды — лист выводов |
| | Узлы ввода, люки, короба | | | | | | | |
| 33 | Кран шаровой латунный Ду15 PN16 (отключение ввода) | аналог | | выбор заказчика | шт | 6 | | Ст В1-1, Ст Т3-1, Ст В1-2, Ст Т3-2, Ст В1-3, Ст Т3-3 |
| 34 | Фильтр сетчатый косой Ду15 | аналог | | выбор заказчика | шт | 6 | | |
| 35 | Счётчик воды крыльчатый Ду15 (ХВ, ГВ), с поверкой | аналог | | выбор заказчика | шт | 6 | | пломба УК |
| 36 | Клапан обратный Ду15 | аналог | | выбор заказчика | шт | 6 | | |
| 37 | Люк ревизионный нажимной под плитку 300×400 мм | аналог | | выбор заказчика | шт | 3 | | к стоякам и арматуре |
| 38 | Звукоизоляция стояка К1 в коробе: рулонный звукоизоляционный материал ≥ 10 мм, обмотка стояка на высоту этажа | аналог | | выбор заказчика | м | 8,4 | | Ст К1-1, Ст К1-2 (кухня), Ст К1-3 |
| 39 | Короб К1 над полом: профиль ПН/ПС, ГКЛВ 12,5 мм под плитку | аналог | | выбор заказчика | м | 11,6 | | сечение — лист разводки |

## Примечания

1. Форма 1 ГОСТ 21.110-2013, ширины граф изменены по п. 4.1. «Аналог» — аналог по характеристикам: модели внести до черновых работ, привязки выводов сверить по паспортам.
2. Бытовая техника не входит (показана арматура подключения), мойка — в комплекте кухни. Длины труб — трасса листа разводки + подъёмы + 10 %.
3. Стояк К1 в коробе — звукоизоляция стояка в коробе без жёсткого контакта короба с трубой.
4. Расчёт систем водоснабжения и канализации, диаметры магистралей и подбор оборудования выполняет проектная организация.

| | | | | | | |
|---|---|---|---|---|---|---|
| | | | | | Проект: Дом 331 м² | |
| | Лист | № док. | Подпись | Дата | | |
| Дизайнер | Кырлан А.С. | | | 19.10.26 | Спецификация сантехнического оборудования | Стадия: П; Лист: 24; Листов: 156 |

выпуск 18.10.2026 № 8cd922c868 · стр. 24 из 156

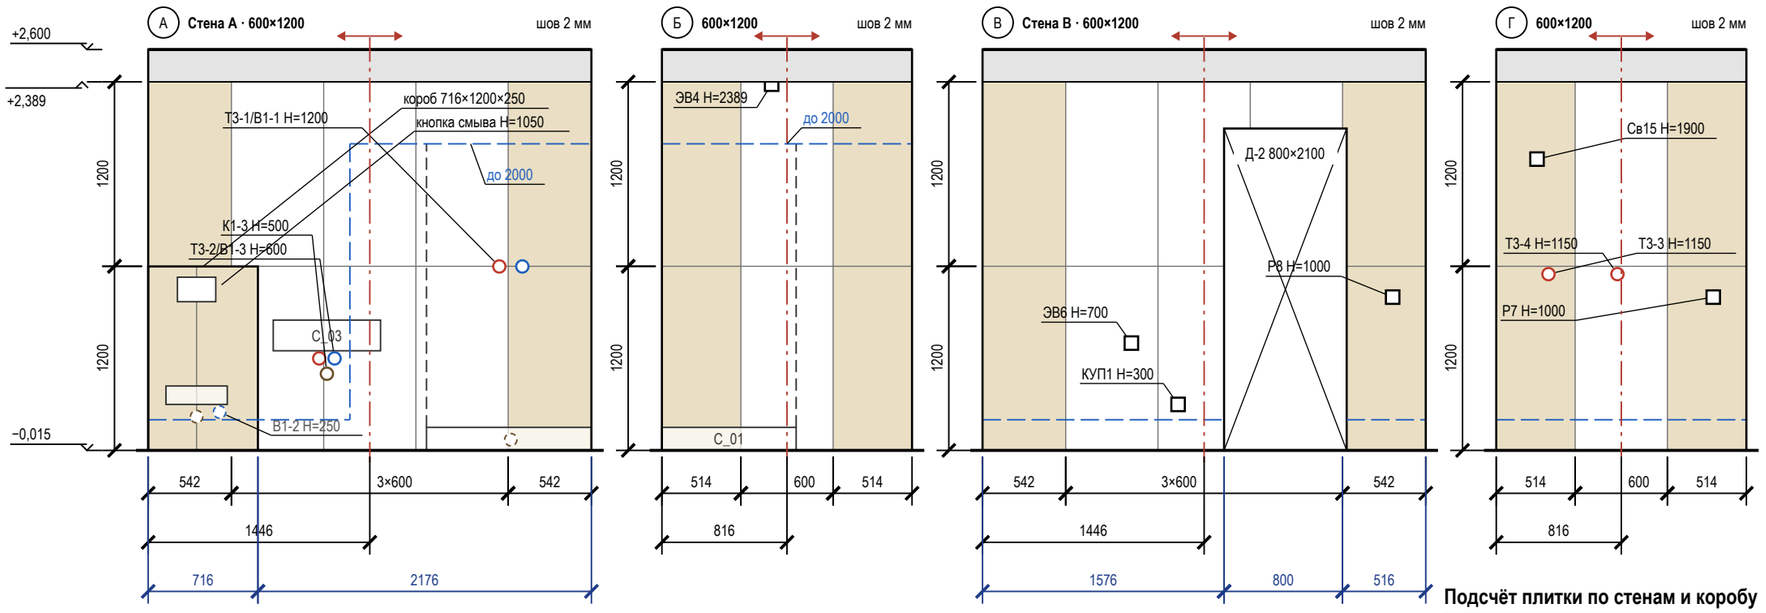


## Условные обозначения

- плитка целая; тонкая линия — шов
- плитка с подрезкой (размер — на цепочке)
- ось старта; стрелки — направление укладки
- верх гидроизоляции: 200 от ЧП, в мокрой зоне — «до …»
- проём — не облицовывается
- сантехприбор: габарит, высота по практике
- граница душевой зоны (ограждение)
- короб инсталляции, в нём кнопка смыва 250×160
- вывод В1 (код — в ведомости привязок)
- вывод Т3 (код — в ведомости привязок)
- вывод К1 (код — в ведомости привязок)
- вывод за прибором / в коробе (не на сетке)
- электроточка: марка и Н — по листам ЭОМ
- отметка уровня, м: ±0,000 — чистый пол жилых помещений
- низ потолка; серая полоса — стена без плитки
- А — обозначение стены А–Г (как на развёртках)

## Примечания

1. Вид изнутри, стены по часовой стрелке А → Г. Высоты — от чистого пола (−0,015), отметки — от ±0,000. Раскладка от чистовых размеров (штукатурка 10 + клей 5 + плитка 9 мм), подрезки чистые; старт — от оси стены, ряды от пола целыми.
2. Верх плитки +2,389, потолок +2,600, зазор 211 мм: потолок ГКЛ опустить до +2,392 (шов 3 мм, герметик) согласовать с монтажником ГКЛ; иначе профиль-окантовка, полосу окрасить в цвет потолка. Подрезной ряд 206 мм не делать.
3. Точки из таблицы сдвигов переносятся до черновой разводки: смеситель — по оси пары В1 + Т3; вывод на оси прибора — вместе с прибором, иначе старт раскладки — на ось прибора.
4. За приборами и в коробе (К1-1, В1-2, К1-2) — штриховым кольцом.
5. Гидроизоляция: 200 мм от ЧП по периметру; у душа — до 2000 и 500 мм за поддон (СП 29.13330.2011, п. 7.2 — на высоту замачивания); углы — лентой; акт скрытых работ, пролив.
6. Короб 716×1200×250: лицо 315 / 399 мм от оси кнопки смыва, боковины, полка; углы — запил 45° или профиль; за коробом плитку не кладут.

## Подсчёт плитки по стенам и коробу

| Поверхность | L × H, мм | S, м² | Целых | Подр. | С запасом | Подрезки: край / верх, мм |
|---|---|---|---|---|---|---|
| стена А | 2892 × 2404 | 6,21 | 5 | 4 | 10 | 542 / 542; целый ряд |
| короб (ст. А) | 716×1200×250 | 1,64 | 0 | 6 | 7 | лицо 315 / 399; бок. 250 |
| стена Б | 1632 × 2404 | 4,04 | 2 | 4 | 7 | 514 / 514; целый ряд |
| стена В | 2892 × 2404 | 5,39 | 2 | 7 | 10 | 542 / 542; целый ряд |
| стена Г | 1632 × 2404 | 4,04 | 2 | 4 | 7 | 514 / 514; целый ряд |
| **Итого** | | **21,31** | **11** | **25** | **41** | |

## Сдвиг точек под раскладку

| Точка (ВК, ЭОМ) | Стена | Проект: от угла / Н | Под раскладку: от угла / Н | Сдвиг, мм |
|---|---|---|---|---|
| Т3-1/В1-1 | А | 2366 / 1200 | 2349 / 1141 | −17 на шов; Н −59 |
| Т3-2/В1-3, К1-3 | А | 1166 / 600, 500 | 1145 / 600, 500 | −21 на шов |
| ЭВ4 | Б | 716 / 2389 | 816 / 2403 | +100 в центр плитки; Н +14 |
| Р8 | В | 2676 / 1000 | 2650 / 1000 | −26 в центр плитки |
| КУП1 | В | 1276 / 300 | 1145 / 300 | −131 на шов |
| ЭВ6 | В | 971 / 700 | 844 / 700 | −127 в центр плитки |
| Т3-3 | Г | 341 / 1150 | 214 / 1150 | −127 в центр плитки |
| Т3-4 | Г | 791 / 1150 | 816 / 1150 | +25 в центр плитки |
| Св15 | Г | 266 / 1900 | 214 / 1900 | −52 в центр плитки |

| | Лист | № док. | Подпись | Дата |
|---|---|---|---|---|
| Дизайнер | Кырлан А.С. | | | 19.10.26 |

Проект: Дом 331 м²

Раскладка плитки. Санузел 1 этажа. Развёртки стен

| Стадия | Лист | Листов |
|---|---|---|
| П | 25 | 156 |

выпуск 18.10.2026 № 8cd922c868 · стр. 25 из 156

Правка к этому листу

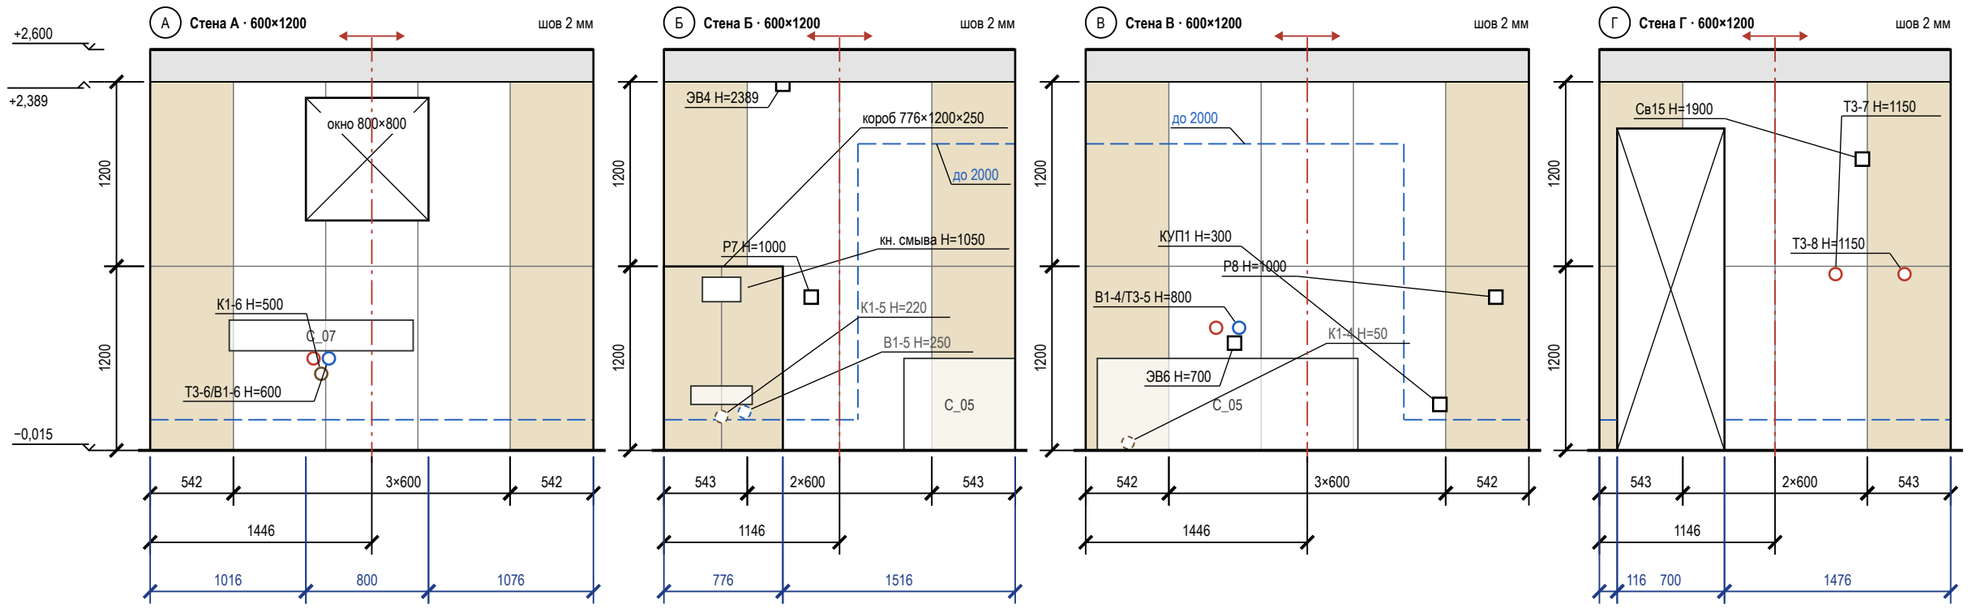


## Подсчёт плитки по стенам и коробу

| Поверхность | L × H, мм | S, м² | Целых | Подр. | С запасом | Подрезки: край / верх, мм |
|---|---|---|---|---|---|---|
| стена А | 2892 × 2404 | 4,54 | 3 | 7 | 11 | 542 / 542; целый ряд |
| стена Б | 2292 × 2404 | 3,97 | 3 | 4 | 8 | 543 / 543; целый ряд |
| короб (ст. Б) | 776×1200×250 | 1,73 | 0 | 6 | 7 | лицо 375 / 399; бок. 250 |
| стена В | 2892 × 2404 | 7,07 | 6 | 4 | 11 | 542 / 542; целый ряд |
| стена Г | 2292 × 2404 | 3,43 | 2 | 6 | 9 | 543 / 543; целый ряд |
| **Итого** | | **20,73** | **14** | **27** | **46** | |

## Сдвиг точек под раскладку

| Точка (ВК, ЭОМ) | Стена | Проект: от угла / Н | Под раскладку: от угла / Н | Сдвиг, мм |
|---|---|---|---|---|
| Т3-6/В1-6, К1-6 | А | 1116 / 600, 500 | 1145 / 600, 500 | +29 на шов |
| Р7 | Б | 961 / 1000 | 845 / 1000 | −116 в центр плитки |
| ЭВ4 | Б | 776 / 2389 | 845 / 2403 | +69 в центр плитки; Н +14 |
| В1-4/Т3-5 | В | 926 / 800 | 844 / 800 | −82 в центр плитки |
| Р8 | В | 2676 / 1000 | 2650 / 1000 | −26 в центр плитки |
| КУП1 | В | 2311 / 300 | 2349 / 300 | +38 на шов |
| ЭВ6 | В | 971 / 700 | 844 / 700 | −127 в центр плитки |
| Т3-7 | Г | 1541 / 1150 | 1447 / 1150 | −94 в центр плитки |
| Т3-8 | Г | 1991 / 1150 | 2049 / 1150 | +58 в центр плитки |
| Св15 | Г | 1716 / 1900 | 1748 / 1900 | +32 на шов |

## Условные обозначения

- плитка целая; тонкая линия — шов
- плитка с подрезкой (размер — на цепочке)
- ось старта; стрелки — направление укладки
- верх гидроизоляции: 200 от ЧП, в мокрой зоне — «до …»
- проём — не облицовывается
- сантехприбор: габарит, высота по практике
- короб инсталляции, в нём кнопка смыва 250×160
- вывод В1 (код — в ведомости привязок)
- вывод Т3 (код — в ведомости привязок)
- вывод К1 (код — в ведомости привязок)
- вывод за прибором / в коробе (не на сетке)
- электроточка: марка и Н — по листам ЭОМ
- отметка уровня, м: ±0,000 — чистый пол жилых помещений
- низ потолка; серая полоса — стена без плитки
- А — обозначение стены А–Г (как на развёртках)

## Примечания

1. Вид изнутри, стены по часовой стрелке А → Г. Высоты — от чистого пола (−0,015), отметки — от ±0,000. Раскладка от чистовых размеров (штукатурка 10 + клей 5 + плитка 9 мм), подрезки чистые; старт — от оси стены, ряды от пола целыми.
2. Верх плитки +2,389, потолок +2,600, зазор 211 мм: потолок ГКЛ опустить до +2,392 (шов 3 мм, герметик) — согласовать с монтажником ГКЛ; иначе профиль-окантовка, полосу окрасить в цвет потолка. Подрезной ряд 206 мм не делать.
3. Точки из таблицы сдвигов переносятся до черновой разводки: смеситель — по оси пары В1 + Т3; вывод на оси прибора вместе с прибором, иначе старт раскладки — на ось прибора.
4. За приборами и в коробе (В1-5, К1-5, К1-4) — штриховым кольцом.
5. Гидроизоляция: 200 мм от ЧП по периметру; над ванной — до 2000 и 300 мм за борт (СП 29.13330.2011, п. 7.2 — на высоту замачивания); углы — лентой; акт скрытых работ, пролив.
6. Короб 776×1200×250: лицо 375 / 399 мм от оси кнопки смыва, боковины, полка; углы — запил 45° или профиль; за коробом плитку не кладут.

| | | | | | |
|---|---|---|---|---|---|
| | | | | | Проект: Дом 331 м² |
| | Лист | № док. | Подпись | Дата | Раскладка плитки. Санузел мастер. Развёртки стен |
| Дизайнер | Кырлан А.С. | | | 19.10.26 | |

| Стадия | Лист | Листов |
|---|---|---|
| П | 26 | 156 |

выпуск 18.10.2026 № 8cd922c868 · стр. 26 из 156

Правка к этому листу

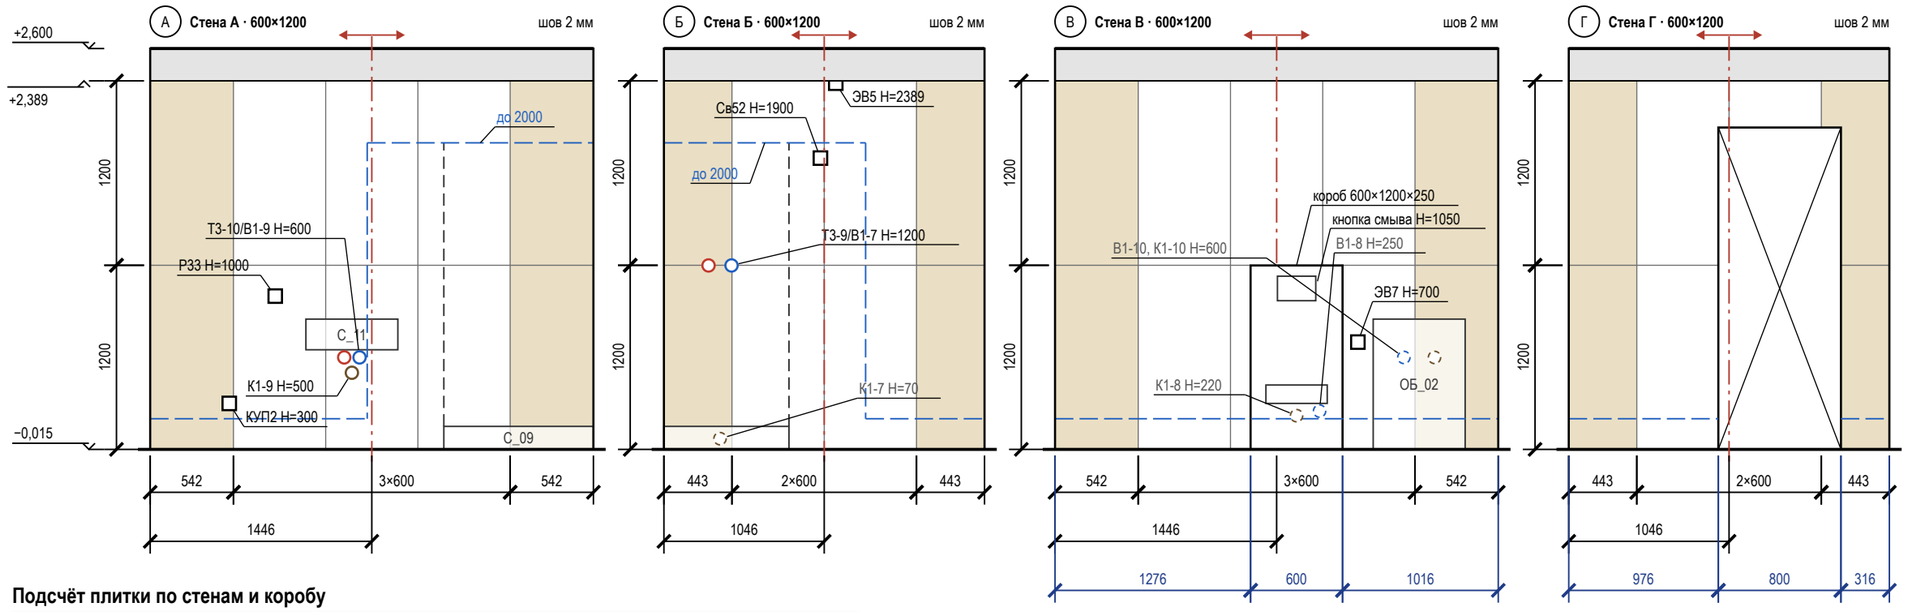


## Подсчёт плитки по стенам и коробу

| Поверхность | L × H, мм | S, м² | Целых | Подр. | С запасом | Подрезки: край / верх, мм |
|---|---|---|---|---|---|---|
| стена А | 2892 × 2404 | 7,07 | 6 | 4 | 11 | 542 / 542; целый ряд |
| стена Б | 2092 × 2404 | 4,42 | 4 | 4 | 9 | 443 / 443; целый ряд |
| стена В | 2892 × 2404 | 2,81 | 4 | 6 | 11 | 542 / 542; целый ряд |
| короб (ст. В) | 600×1200×250 | 1,47 | 1 | 3 | 5 | лицо 600; бок. 250 |
| стена Г | 2092 × 2404 | 2,74 | 0 | 7 | 8 | 443 / 443; целый ряд |
| **Итого** | | **18,51** | **15** | **24** | **44** | |

## Сдвиг точек под раскладку

| Точка (ВК, ЭОМ) | Стена | Проект: от угла / Н | Под раскладку: от угла / Н | Сдвиг, мм |
|---|---|---|---|---|
| Т3-10/В1-9, К1-9 | А | 1316 / 600, 500 | 1446 / 600, 500 | +130 в центр плитки |
| Р33 | А | 816 / 1000 | 844 / 1000 | +28 в центр плитки |
| КУП2 | А | 516 / 300 | 543 / 300 | +27 на шов |
| Т3-9/В1-7 | Б | 366 / 1200 | 444 / 1141 | +78 на шов; Н −59 |
| Св52 | Б | 1021 / 1900 | 1046 / 1900 | +25 на шов |
| ЭВ5 | Б | 1121 / 2389 | 1046 / 2343 | −75 на шов; Н −46 |
| ЭВ7 | В | 1976 / 700 | 2048 / 700 | +72 в центр плитки |

## Условные обозначения

- плитка целая; тонкая линия — шов
- плитка с подрезкой (размер — на цепочке)
- ось старта; стрелки — направление укладки
- верх гидроизоляции: 200 от ЧП, в мокрой зоне — «до …»
- проём — не облицовывается
- сантехприбор: габарит, высота по практике
- граница душевой зоны (ограждение)
- короб инсталляции, в нём кнопка смыва 250×160
- вывод В1 (код — в ведомости привязок)
- вывод Т3 (код — в ведомости привязок)
- вывод К1 (код — в ведомости привязок)
- вывод за прибором / в коробе (не на сетке)
- электроточка: марка и Н — по листам ЭОМ
- отметка уровня, м: ±0,000 — чистый пол жилых помещений
- низ потолка; серая полоса — стена без плитки
- (А) обозначение стены А–Г (как на развёртках)

## Примечания

1. Вид изнутри, стены по часовой стрелке А → Г. Высоты — от чистого пола (−0,015), отметки — от ±0,000. Раскладка от чистовых размеров (штукатурка 10 + клей 5 + плитка 9 мм), подрезки чистые; старт — от оси стены, ряды от пола целыми.
2. Верх плитки +2,389, потолок +2,600, зазор 211 мм: потолок ГКЛ опустить до +2,392 (шов 3 мм, герметик) согласовать с монтажником ГКЛ; иначе профиль-окантовка, полосу окрасить в цвет потолка. Подрезной ряд 206 мм не делать.
3. Точки из таблицы сдвигов переносятся до черновой разводки: смеситель — по оси пары В1 + Т3; вывод на оси прибора — вместе с прибором, иначе старт раскладки — на ось прибора.
4. За приборами и в коробе (К1-7, В1-8, К1-8, В1-10, К1-10) — штриховым кольцом.
5. Гидроизоляция: 200 мм от ЧП по периметру; у душа — до 2000 и 500 мм за поддон (СП 29.13330.2011, п. 7.2 — на высоту замачивания); углы — лентой; акт скрытых работ, пролив.
6. Короб 600×1200×250: лицо 600 мм от оси кнопки смыва, боковины, полка; углы — запил 45° или профиль; за коробом плитку не кладут.

| | | | | | |
|---|---|---|---|---|---|
| | | | | | Проект: Дом 331 м² |
| | Лист | № док. | Подпись | Дата | Раскладка плитки. Санузел 2. Развёртки стен |
| Дизайнер | Кырлан А.С. | | | 19.10.26 | |

| Стадия | Лист | Листов |
|---|---|---|
| П | 27 | 156 |

Правка к этому листу

## Примечания

1. Размеры проёмов и привязки — в миллиметрах от чистых граней стен до отделки; привязка — от угла того помещения, со стороны которого стоит размер. Размер в ведомости — ширина × высота проёма от чистого пола 0,000.
2. Марки в кружках — типы заполнения проёмов (ГОСТ 21.501-2018, п. 5.3.2); одна марка — один типоразмер; количество сверено с планом.
3. Открывание: Л — петли слева, П — справа, если смотреть со стороны, куда открывается полотно (на себя).
4. Дверные блоки обычного монтажа (Д-4…Д-6, Д-14) заказывать после чистовой стяжки и штукатурки, проёмы перемерить; монтажный зазор коробки 10–15 мм на сторону, откос от угла помещения до коробки не менее 50 мм.
5. Скрытые двери (Д-1, Д-2): проём замерить в чистоте; блок заказать до штукатурки (≈ 30 дн.), короб ставить до штукатурки; полотно навесить после чистовой отделки, красить в цвет стен. Порядок практика монтажа, изготовитель подтверждает.
6. Д-1, Д-2 — существующие проёмы, до техзаключения не расширять.

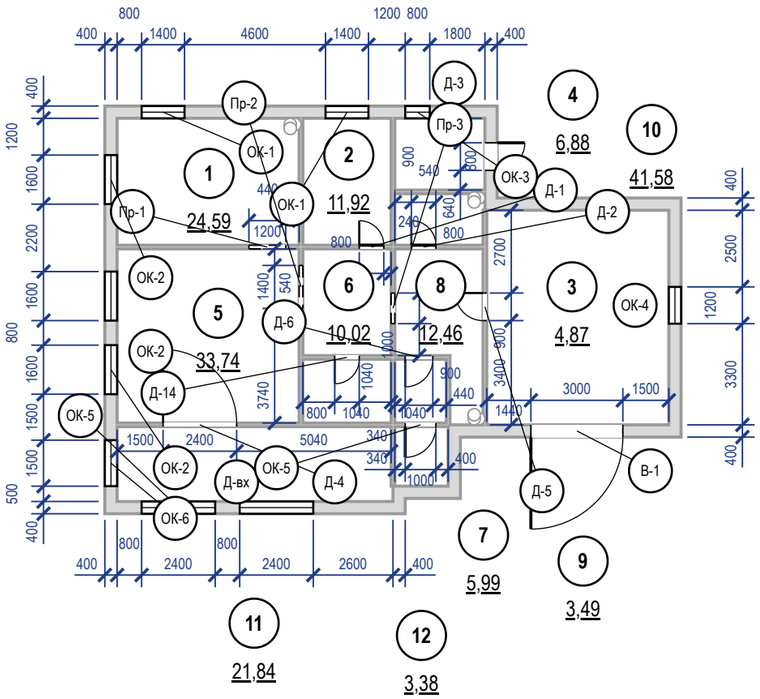


## Ведомость заполнения проёмов

| Марка | Наименование, обозначение | Проём ш×в, мм | Кол. | Откр. | Отделка полотна | Фурнитура | Прим. |
|---|---|---|---|---|---|---|---|
| Д-вх | Блок дверной входной, ГОСТ 31173-2016 | 1000×2100 | 1 | Л | в комплекте блока | в комплекте блока (замки, глазок) | наружу |
| В-1 | Блок дверной входной, ГОСТ 31173-2016 | 3000×2300 | 1 | Л | в комплекте блока | в комплекте блока (замки, глазок) | наружу |
| Д-1 | Дверь скрытого монтажа, ТУ изготовителя | 800×2100 | 1 | П | окраска No. 226 с двух сторон | скрытые петли 3D, магнитный замок | |
| Д-2 | Дверь скрытого монтажа, ТУ изготовителя | 800×2100 | 1 | П | в тон облицовки — пом. 3, No. 226 — пом. 8 | скрытые петли 3D, магнитный замок, фиксатор WC | порог 15 |
| Д-3 | Блок дверной входной, ГОСТ 31173-2016 | 900×2100 | 1 | П | в комплекте блока | в комплекте блока (замки, глазок) | наружу |
| Д-4 | Блок дверной внутренний, остекл., ГОСТ 475-2016 | 2400×2100 | 1 | П | | петли, ручка с защёлкой | |
| Д-5 | Блок дверной внутренний, ГОСТ 475-2016 | 900×2100 | 1 | Л | | петли, ручка с защёлкой | |
| Д-6 | Блок дверной внутренний, ГОСТ 475-2016 | 900×2100 | 1 | Л | | петли, ручка с защёлкой | |
| Д-14 | Блок дверной внутренний, ГОСТ 475-2016 | 800×2100 | 1 | Л | | петли, ручка с защёлкой | |
| Пр-1 | Портал без заполнения | 1200×2100 | 1 | | | | б/п |
| Пр-2 | Портал без заполнения | 1400×2100 | 1 | | | | б/п |
| Пр-3 | Портал без заполнения | 1000×2100 | 1 | | | | б/п |
| ОК-1 | Блок оконный, ГОСТ 23166-2021 | 1400×1500 | 2 | | | | низ 900 |
| ОК-2 | Блок оконный, ГОСТ 23166-2021 | 1600×1500 | 3 | | | | низ 900 |
| ОК-3 | Блок оконный, ГОСТ 23166-2021 | 800×900 | 1 | | | | низ 1200 |
| ОК-4 | Блок оконный, ГОСТ 23166-2021 | 1200×900 | 1 | | | | низ 1200 |
| ОК-5 | Блок оконный, ГОСТ 23166-2021 | 2400×1600 | 2 | | | | низ 900 |
| ОК-6 | Блок оконный, ГОСТ 23166-2021 | 1500×1600 | 1 | | | | низ 900 |

| | | | | | | | |
|---|---|---|---|---|---|---|---|
| | | | | | Проект: Дом 331 м² | | |
| | Лист | № док. | Подпись | Дата | План размещения дверей · 1-й этаж | Стадия | Лист | Листов |
| Дизайнер | Кырлан А.С. | | | 19.10.26 | | П | 28 | 156 |

выпуск 18.10.2026 № 8cd922c868 · стр. 28 из 156

Правка к этому листу

## Примечания

1. Размеры проёмов и привязки — в миллиметрах от чистых граней стен до отделки; привязка — от угла того помещения, со стороны которого стоит размер. Размер в ведомости — ширина × высота проёма от чистого пола 0,000. Откос от угла помещения до проёма с коробкой — не менее 50 мм.
2. Марки в кружках — типы заполнения проёмов (ГОСТ 21.501-2018, п. 5.3.2); одна марка — один типоразмер; количество сверено с планом.
3. Открывание: Л — петли слева, П — справа, если смотреть со стороны, куда открывается полотно (на себя).
4. Скрытые двери (Д-7…Д-13): проём замерить в чистоте; блок заказать до штукатурки (≈ 30 дн.), короб ставить до штукатурки; полотно навесить после чистовой отделки, красить в цвет стен. Порядок практика монтажа, изготовитель подтверждает.
5. Д-7…Д-13 — существующие проёмы, до техзаключения не расширять.

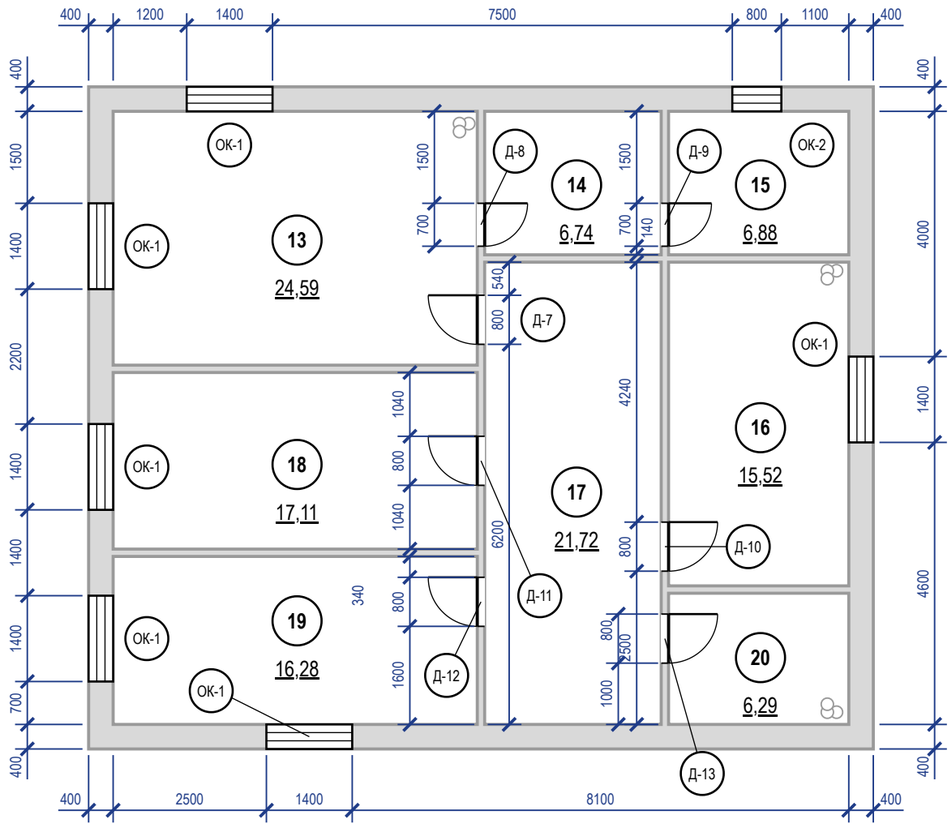


## Ведомость заполнения проёмов

| Марка | Наименование, обозначение | Проём ш×в, мм | Кол. | Откр. | Отделка полотна | Фурнитура | Прим. |
|---|---|---|---|---|---|---|---|
| Д-7 | Дверь скрытого монтажа, ТУ изготовителя | 800×2100 | 1 | Л | окраска No. 226 с двух сторон | скрытые петли 3D, магнитный замок | |
| Д-8 | Дверь скрытого монтажа, ТУ изготовителя | 700×2100 | 1 | П | No. 105 — пом. 14, No. 226 — пом. 13 | скрытые петли 3D, магнитный замок | |
| Д-9 | Дверь скрытого монтажа, ТУ изготовителя | 700×2100 | 1 | П | в тон облицовки — пом. 15, No. 105 — пом. 14 | скрытые петли 3D, магнитный замок, фиксатор WC | порог 15 |
| Д-10 | Дверь скрытого монтажа, ТУ изготовителя | 800×2100 | 1 | П | окраска No. 226 с двух сторон | скрытые петли 3D, магнитный замок | |
| Д-11 | Дверь скрытого монтажа, ТУ изготовителя | 800×2100 | 1 | Л | окраска No. 226 с двух сторон | скрытые петли 3D, магнитный замок | |
| Д-12 | Дверь скрытого монтажа, ТУ изготовителя | 800×2100 | 1 | Л | окраска No. 226 с двух сторон | скрытые петли 3D, магнитный замок | |
| Д-13 | Дверь скрытого монтажа, ТУ изготовителя | 800×2100 | 1 | П | в тон облицовки — пом. 20, No. 226 — пом. 17 | скрытые петли 3D, магнитный замок, фиксатор WC | порог 15 |
| ОК-1 | Блок оконный, ГОСТ 23166-2021 | 1400×1500 | 6 | | | | низ 900 |
| ОК-2 | Блок оконный, ГОСТ 23166-2021 | 800×800 | 1 | | | | низ 1500 |

| | | | | | | | |
|---|---|---|---|---|---|---|---|
| | | | | | Проект: Дом 331 м² | | |
| | Лист | № док. | Подпись | Дата | План размещения дверей · Мансарда | Стадия | Лист | Листов |
| Дизайнер | Кырлан А.С. | | | 19.10.26 | | П | 29 | 156 |

Правка к этому листу

## План марша Л-1 (М 1:50) · 6. Холл с лестницей

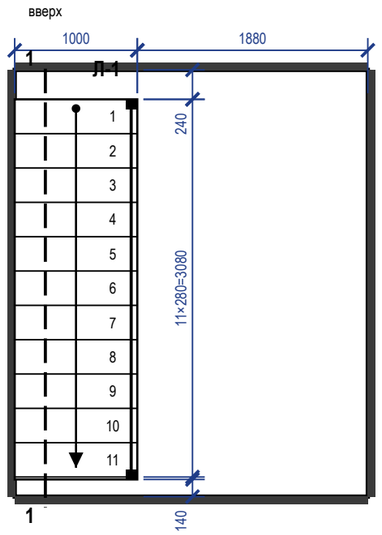


## Разрез 1-1 (М 1:50)

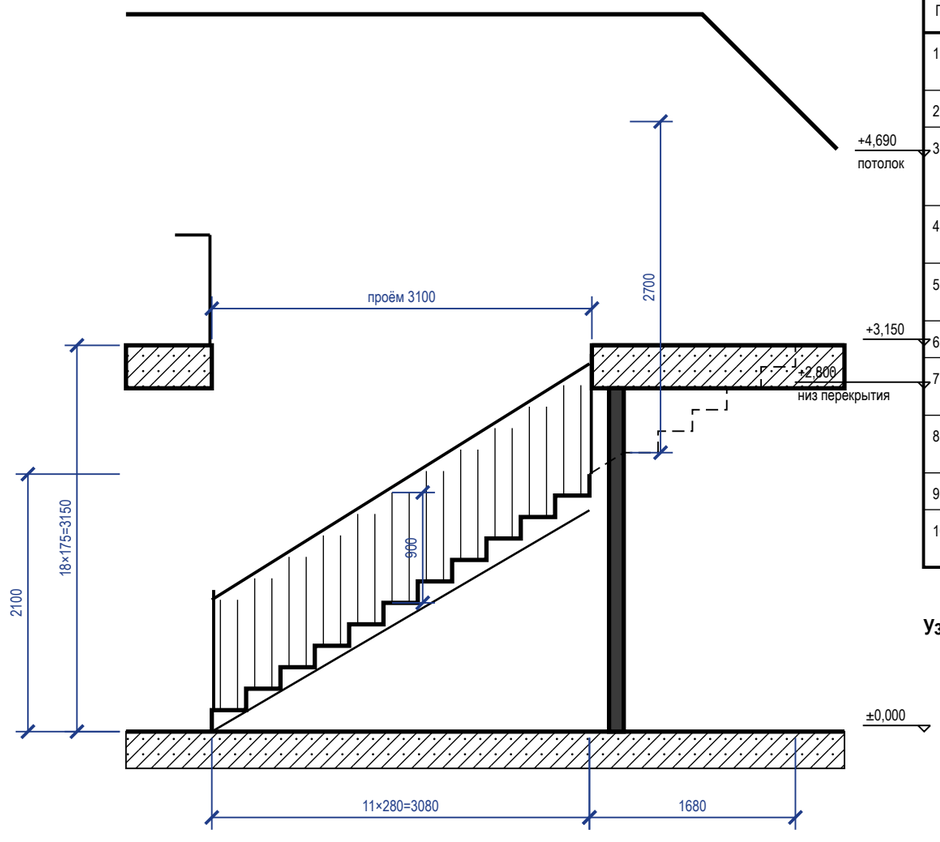


## Спецификация элементов лестницы Л-1

| Поз. | Наименование | Кол. | Материал, сечение | Примечание |
|---|---|---|---|---|
| 1 | Ступень (проступь) | 17 | дуб, массив 40 мм, масло | 1000×280, толщина по изделию |
| 2 | Подступенок | 18 | дуб 18 мм | высота 175 |
| 3 | Косоур | 2 | косоуры стальные 80×40×4, порошковая окраска | несущие марша |
| 4 | Столб ограждения марша | 2 | сталь 20×20, порошковая окраска | по концам марша, стороны Б |
| 5 | Балясина | 46 | сталь 20×20, порошковая окраска | шаг 120, просвет 100 |
| 6 | Поручень марша | 1 | дуб 40×60 | L ≈ 5,61 м, h 900 |
| 7 | Столб ограждения проёма | 3 | сталь 20×20, порошковая окраска | углы проёма, стороны А, Б |
| 8 | Балясина ограждения проёма | 34 | сталь 20×20, порошковая окраска | шаг 120 |
| 9 | Поручень ограждения проёма | 1 | дуб 40×60 | L ≈ 4,10 м, h 900 |
| 10 | Крепёж ограждения | 1 | комплект по изделию | нагрузка на поручень 0,5 кН/м |

## Узел 1. Крепление стойки ограждения (М 1:5)

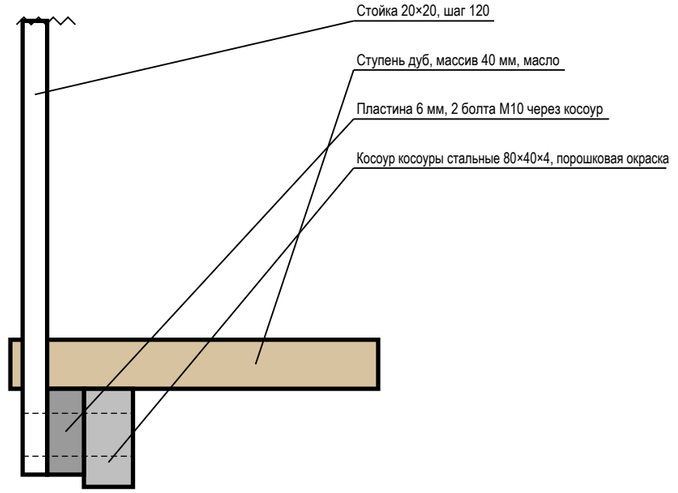


Зазор заполнения до ступени 100 (ГОСТ 25772, прил. А); узел типовой, уточнить по изделию

## Примечания

1. Лестница Л-1: 18 подъёмов × 175 мм = 3150 мм (отм. ±0,000 … +3,150), проступь 280 мм, ширина марша 1000 мм; уклон 32,0°, шаг 2h + b = 630 мм (удобно 600–640 — практика).
2. В габарит марша 3100 мм входят 11 проступей (до отм. +2,100); до пола этажа выше нужно 17 проступей — 4760 мм (показаны штрихом): одномаршевая лестница в этом помещении не встаёт, решение по реестру.
3. Ограждение марша со стороны Б: балясины, просвет между элементами 100 мм (не больше 150 — ГОСТ 25772-2025, табл. 3, тип МВ); высота 900 мм, поручень с одной стороны на 900 мм по линии носков (не менее 900 — СП 55.13330.2016, п. 8.3; СП 59.13330.2020, п. 6.2.11).
4. Проём в перекрытии 1000×3100 мм на этаже 2 ограждён со сторон А, Б высотой 900 мм, непрерывно, с поручнем (СП 55.13330.2016, п. 8.3); нагрузка на поручень 0,5 кН/м (СП 20.13330.2016, п. 8.2.6).
5. Просвет над линией носков — не менее 2700 мм (ступень 13, под потолком мансарды); рекомендуется не менее 2000, путь эвакуации — 2200 (СП 55.13330.2016, п. 7.4).
6. Все подступенки одной высоты (СП 55.13330.2016, п. 8.2). Размеры по месту уточнить после обмера: разность отметок чистых полов замерить до заказа изделия.
7. Узел 1 — типовое решение крепления стойки к косоуру; крепёж, сечения и материал — по проекту изделия изготовителя лестницы.

| | | | | | |
|---|---|---|---|---|---|
| | | | | | Проект: Дом 331 м² |
| | Лист | № док. | Подпись | Дата | |
| Дизайнер | Кырлан А.С. | | | 19.10.26 | Лестница Л-1 |
| | | | | | Стадия: П; Лист: 30; Листов: 156 |

выпуск 18.10.2026 № 8cd922c868 · стр. 30 из 156

Правка к этому листу

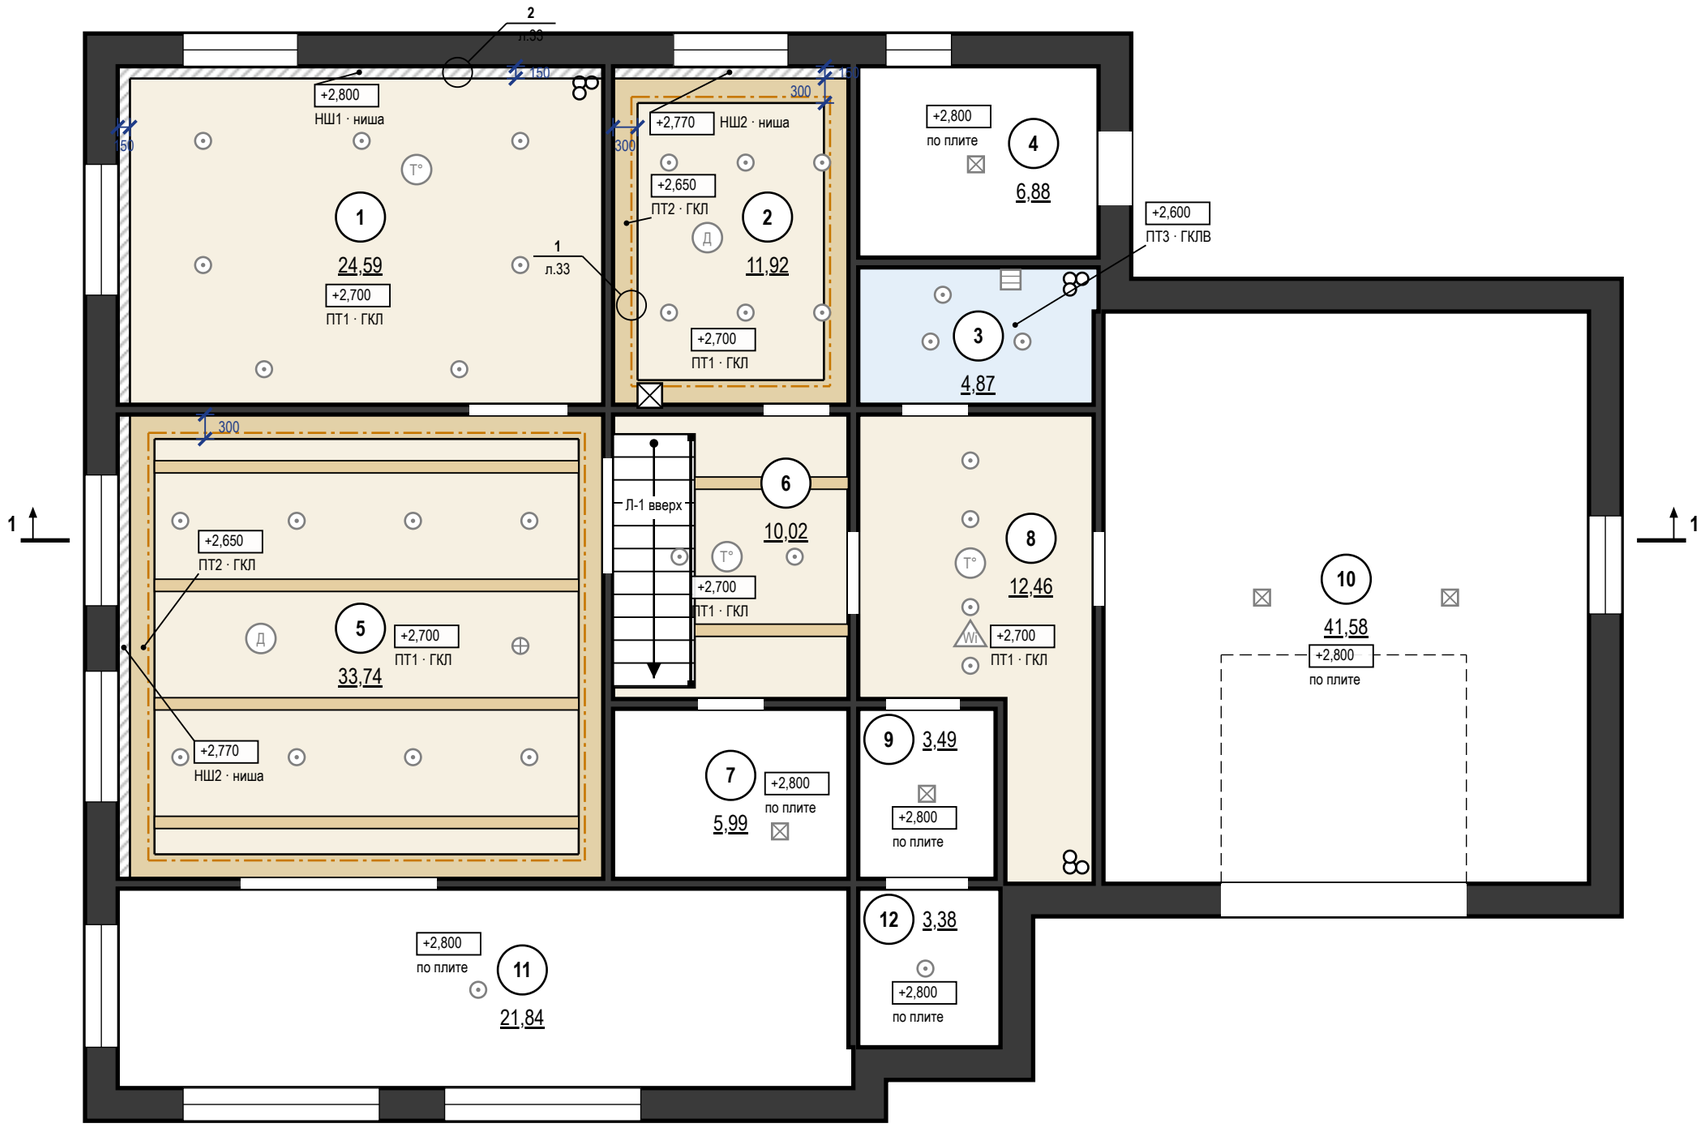


## Ведомость потолков

| Пом. | Марка | Конструкция | Низ | S, м² | Q |
|---|---|---|---|---|---|
| 1 | ПТ1 | ГКЛ П113 | +2,700 | 23,10 | Q3 |
| 1 | НШ1 | ниша под шторы 150×100 | +2,800 | 1,49 | |
| 2 | ПТ2 | ГКЛ П113, короб LED | +2,650 | 3,76 | Q3 |
| 2 | ПТ1 | ГКЛ П113 | +2,700 | 7,73 | Q3 |
| 2 | НШ2 | ниша под шторы 150×120 | +2,770 | 0,43 | |
| 3 | ПТ3 | ГКЛВ П113 | +2,600 | 4,87 | Q3 |
| 4 | | по плите, окраска | +2,800 | 6,88 | |
| 5 | ПТ2 | ГКЛ П113, короб LED | +2,650 | 6,52 | Q3 |
| 5 | ПТ1 | ГКЛ П113 | +2,700 | 26,37 | Q3 |
| 5 | НШ2 | ниша под шторы 150×120 | +2,770 | 0,85 | |
| 6 | ПТ1 | ГКЛ П113 | +2,700 | 10,02 | Q3 |
| 7 | | по плите, окраска | +2,800 | 5,99 | |
| 8 | ПТ1 | ГКЛ П113 | +2,700 | 12,46 | Q3 |
| 9 | | по плите, окраска | +2,800 | 3,49 | |
| 10 | | по плите, окраска | +2,800 | 41,58 | |
| 11 | | по плите, окраска | +2,800 | 21,84 | |
| 12 | | по плите, окраска | +2,800 | 3,38 | |
| | | **Итого** | | **180,76** | |

## Ведомость вырезов и закладных в потолке

| Марка | Устройство | Кол. | Пом. |
|---|---|---|---|
| | Светильник встраиваемый (марки — план освещения) | 32 | 1, 2, 3, 5, 6, 8, 11, 12 |
| | Светильник накладной (марки — план освещения) | 5 | 4, 7, 9, 10 |
| | Светильник подвесной (марки — план освещения) | 1 | 5 |
| ИП2, ИП1 | Извещатель дымовой | 2 | 2, 5 |
| ИП4, ИП6, ИП3 | Извещатель тепловой | 3 | 1, 6, 8 |
| AP1 | Точка доступа Wi-Fi, PoE | 1 | 8 |
| ВР2 | Решётка вытяжная (вентилятор) | 1 | 3 |
| | Люк ревизии 300×300 | 1 | 2 |

## Примечания

1. За отметку ±0,000 принят уровень чистого пола сухих помещений (готовое покрытие), а не существующего пола; пол пом. 3, 11, 12 — −0,015, −0,030; существующий пол снимается до плиты, его отметка не замерена. Отметки в прямоугольниках — низ потолка; низ плиты перекрытия +2,800. Марка потолка — одна конструкция и отметка на весь альбом.
2. Потолки ГКЛ — каркасная система П113: подвесы через 1000, несущие профили через 500, основные через 1200 мм; листы — поперёк несущих профилей. В помещениях 3 — ГКЛВ на оцинкованном каркасе.
3. Нижний уровень — пояс-короб по периметру шириной 300 мм (карниз подсветки + 150 мм полки), верхний — поле внутри пояса.
4. LED-лента в алюминиевом профиле посередине карниза короба шириной 300 мм (узел 1, лист 33); длина по плану: пом. 2 — 11,9 м (в плане освещения 11,9); пом. 5 — 21,1 м (в плане освещения 21,1).
5. Балки декоративные 150×120 мм, фальш-балка, массив лиственницы под маслом: пом. 5 — 4 шт., 20,8 м; пом. 6 — 2 шт., 3,8 м, низ +2,580; крепление — на закладной брус 50×50 к каркасу П113, саморезы скрыто.
6. Ниши под шторы 150×100 мм — на всю длину стены с окном; карниз — на закладной до обшивки (узел 2, лист 33).
7. Примыкание к стенам: теневой шов 15 мм, техзазор 3 мм — пом. 2, 5, по стенам, выровненным штукатуркой (узел 1); пом. 1, 3, 6, 8 разделительная лента.
8. Светильники и потолочные устройства — подложка с планов освещения, слаботочных систем и вентиляции (положение — по ним); вырезы и закладные — по ведомости на листе, до обшивки; отверстия не совмещать с профилями, глубина корпуса светильника до 70 мм.
9. Разрезы 1–1 и узлы — на листе 33; высоты мебели и дверных блоков сверены с низом потолка в разрезах.
10. Шпаклевание ГКЛ и условия приёмки — Q3: рассеянный дневной свет, осмотр с 2 м; боковой свет не оценивается.
11. Люки ревизии 300×300 мм — по центру блоков питания LED (БП2; координаты — план освещения).
12. Пом. 4, 7, 9, 10, 11, 12 — потолок по плите без подвесной системы; отделка — по ведомости отделки.

| | | | | | |
|---|---|---|---|---|---|
| | | | | | Проект: Дом 331 м² |
| | Лист | № док. | Подпись | Дата | План потолков · 1-й этаж |
| Дизайнер | Кырлан А.С. | | | 19.10.26 | |

| Стадия | Лист | Листов |
|---|---|---|
| П | 31 | 156 |

выпуск 18.10.2026 № 8cd922c868 · стр. 31 из 156

Правка к этому листу

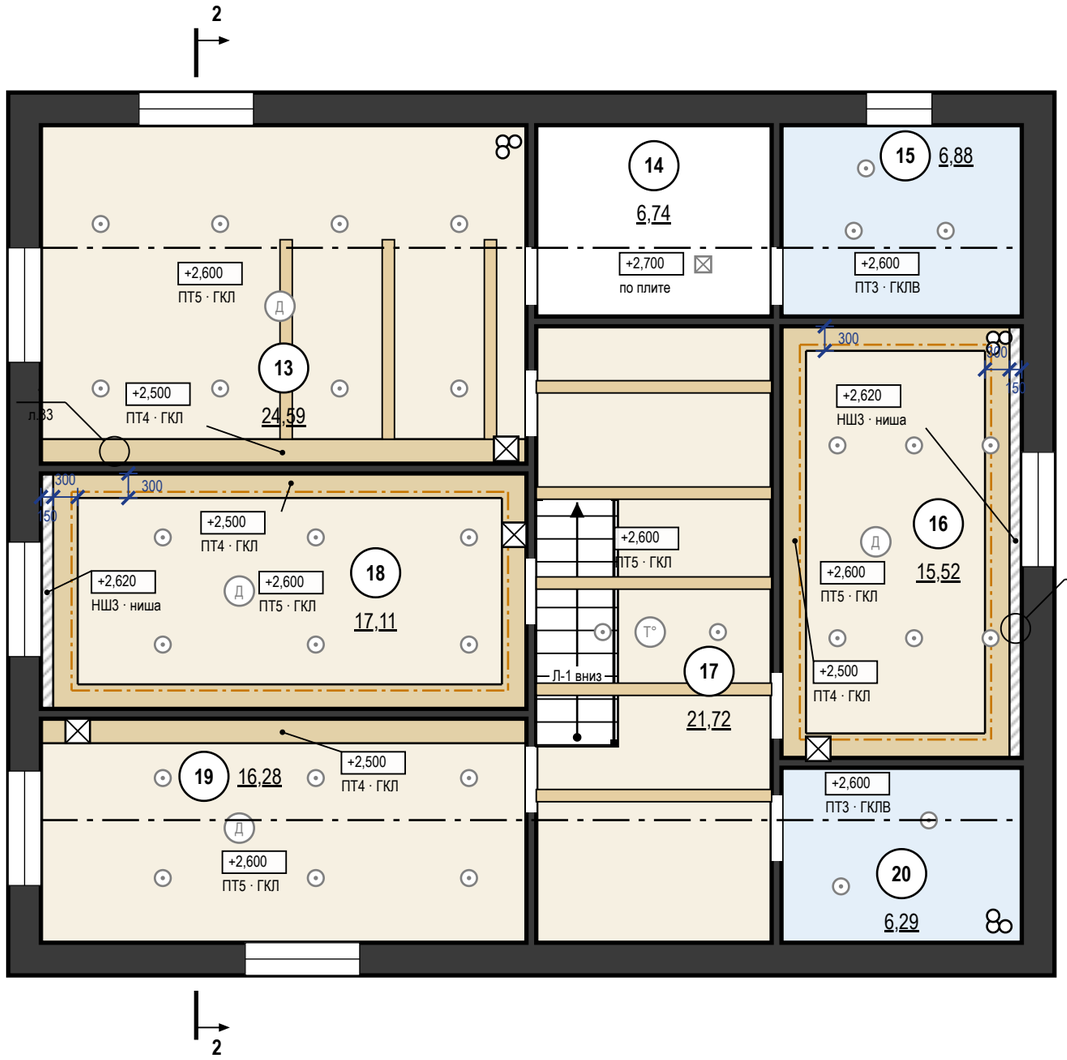


## Ведомость потолков

| Пом. | Марка | Конструкция | Низ | S, м² | Q |
|---|---|---|---|---|---|
| 13 | ПТ4 | ГКЛ П113, короб LED | +2,500 | 1,78 | Q3 |
| 13 | ПТ5 | ГКЛ П113 | +2,600 | 22,81 | Q3 |
| 14 | | по плите, окраска | +2,700 | 6,74 | |
| 15 | ПТ3 | ГКЛВ П113 | +2,600 | 6,88 | Q3 |
| 16 | ПТ4 | ГКЛ П113, короб LED | +2,500 | 4,48 | Q3 |
| 16 | ПТ5 | ГКЛ П113 | +2,600 | 10,25 | Q3 |
| 16 | НШ3 | ниша под шторы 150×120 | +2,620 | 0,79 | |
| 17 | ПТ5 | ГКЛ П113 | +2,600 | 21,72 | Q3 |
| 18 | ПТ4 | ГКЛ П113, короб LED | +2,500 | 4,84 | Q3 |
| 18 | ПТ5 | ГКЛ П113 | +2,600 | 11,84 | Q3 |
| 18 | НШ3 | ниша под шторы 150×120 | +2,620 | 0,43 | |
| 19 | ПТ4 | ГКЛ П113, короб LED | +2,500 | 1,78 | Q3 |
| 19 | ПТ5 | ГКЛ П113 | +2,600 | 14,50 | Q3 |
| 20 | ПТ3 | ГКЛВ П113 | +2,600 | 6,29 | Q3 |
| | | **Итого** | | **115,13** | |

## Ведомость вырезов и закладных в потолке

| Марка | Устройство | Кол. | Пом. |
|---|---|---|---|
| | Светильник встраиваемый (марки — план освещения) | 33 | 13, 15, 16, 17, 18, 19, 20 |
| | Светильник накладной (марки — план освещения) | 1 | 14 |
| ИП1, ИП2, ИП2, ИП2 | Извещатель дымовой | 4 | 13, 16, 18, 19 |
| ИП6 | Извещатель тепловой | 1 | 17 |
| | Люк ревизии 300×300 | 4 | 13, 16, 18, 19 |

## Примечания

1. За отметку ±0,000 принят уровень чистого пола сухих помещений (готовое покрытие), а не существующего пола; пол пом. 15, 20 — −0,015; верх плиты перекрытия −0,064 — расчётный по пирогу пола, не замерен; существующий пол снимается до плиты, его отметка не замерена. Отметки в прямоугольниках — низ потолка; низ плиты перекрытия +2,700. Марка потолка — одна конструкция и отметка на весь альбом.
2. Мансарда: потолок по скатам кровли — от +1,200 у наружных стен вдоль конька до +2,700 у линий перелома (штрихпунктир), между ними горизонтальная часть +2,700 (в пом. 13, 15, 16, 17, 18, 19, 20 горизонтальная часть подшита ниже — по марке и отметке потолка; скат обшит до линии подшивки); над слуховыми окнами скат поднят до горизонтальной части. Обшивка скатов — по стропилам с пароизоляцией по проекту КР.
3. Потолки ГКЛ — каркасная система П113: подвесы через 1000, несущие профили через 500, основные через 1200 мм; листы — поперёк несущих профилей. В помещениях 15, 20 — ГКЛВ на оцинкованном каркасе.
4. Нижний уровень — пояс-короб по периметру шириной 300 мм (карниз подсветки + 150 мм полки), верхний — поле внутри пояса.
5. LED-лента в алюминиевом профиле посередине карниза короба шириной 300 мм (узел 1, лист 33); длина по плану: пом. 13 — 6,0 м (в плане освещения 6); пом. 16 — 14,3 м (в плане освещения 14,3); пом. 18 — 15,5 м (в плане освещения 15,5); пом. 19 — 6,0 м (в плане освещения 6).
6. Балки декоративные 150×120 мм, фальш-балка, массив лиственницы под маслом: пом. 13 — 3 шт., 7,3 м; пом. 17 — 5 шт., 14,4 м, низ +2,480; крепление — на закладной брус 50×50 к каркасу П113, саморезы скрыто.
7. Ниши под шторы 150×120 мм — на всю длину стены с окном; карниз — на закладной до обшивки (узел 2, лист 33).
8. Примыкание к стенам: теневой шов 15 мм, техзазор 3 мм — пом. 16, 18, по стенам, выровненным штукатуркой (узел 1); пом. 13, 15, 17, 19, 20 разделительная лента.
9. Светильники и потолочные устройства — подложка с планов освещения, слаботочных систем и вентиляции (положение — по ним); вырезы и закладные — по ведомости на листе, до обшивки; отверстия не совмещать с профилями, глубина корпуса светильника до 70 мм.
10. Разрезы 2–2 и узлы — на листе 33; высоты мебели и дверных блоков сверены с низом потолка в разрезах.
11. Шпаклевание ГКЛ и условия приёмки — Q3: рассеянный дневной свет, осмотр с 2 м; боковой свет не оценивается.
12. Люки ревизии 300×300 мм — по центру блоков питания LED (БП1, БП2, БП2, БП2; координаты — план освещения).
13. Пом. 14 — потолок по плите без подвесной системы; отделка — по ведомости отделки.

| | | | | | |
|---|---|---|---|---|---|
| | | | | | Проект: Дом 331 м² |
| | Лист | № док. | Подпись | Дата | |
| Дизайнер | Кырлан А.С. | | | 19.10.26 | План потолков · Мансарда |

| Стадия | Лист | Листов |
|---|---|---|
| П | 32 | 156 |

выпуск 18.10.2026 № 8cd922c868 · стр. 32 из 156

Правка к этому листу

## Разрез 1–1 (М 1:40)

Пом. 5 Гостиная

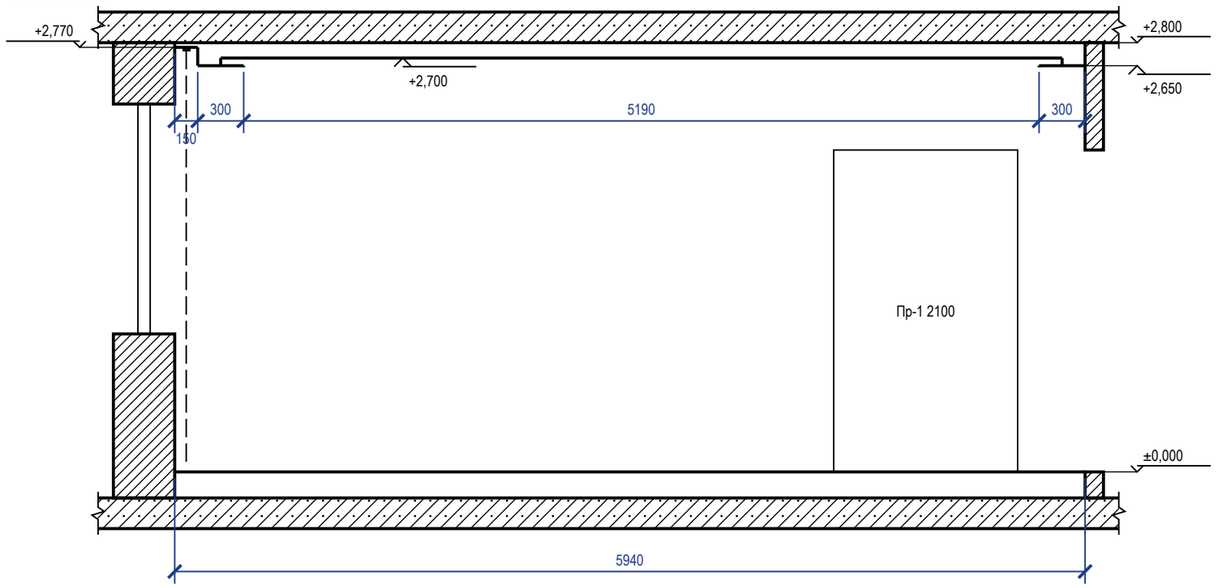


## Разрез 2–2 (М 1:40)

Пом. 13 Спальня мастер

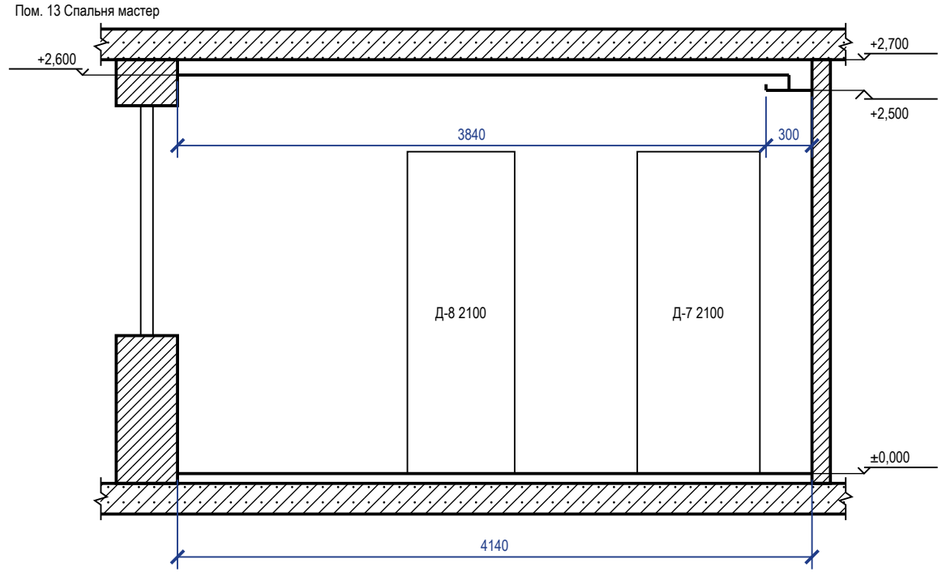


## 1 Короб с LED-подсветкой, теневой шов (М 1:10)

Пом. 2, 5, 13, 16, 18, 19; карниз 150×100, щель под свет 60 мм

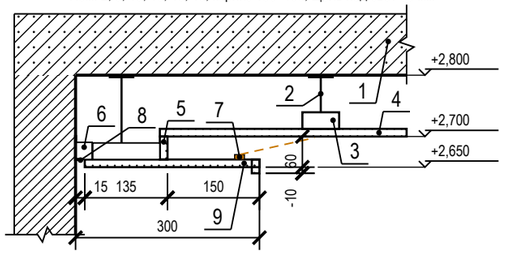


1 — плита перекрытия
2 — подвес прямой, шаг 1000 мм
3 — ПП 60×27: несущие через 500, основные через 1200 мм
4 — ГКЛ 12,5 по П113 — верхний уровень
5 — задняя стенка и бортик карниза — ГКЛ 12,5
6 — ПН 28×27 по периметру, к стене через 500 мм
7 — LED-лента в алюминиевом профиле
8 — теневой профиль: шов 15 мм, зазор 3 мм
9 — низ короба — ГКЛ 12,5 по ПП 60×27

## 2 Ниша под шторы (М 1:10)

Пом. 1, 2, 5, 16, 18; без подсветки; закладные под карниз — до обшивки

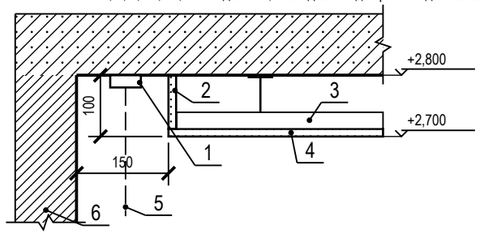


1 — карниз (шина), высота с верхом портьеры 100 мм
2 — стенка ниши — ГКЛ 12,5
3 — ПП 60×27 — каркас короба
4 — низ короба нижнего уровня — ГКЛ 12,5
5 — портьера
6 — стена с окном

## Условные обозначения

- плита перекрытия в сечении
- стена в сечении
- потолок ГКЛ в сечении; под линией — марка потолка (план потолков)
- мебель и дверные проёмы за секущей плоскостью; число — марка и верх от чистого пола, мм
- портьера в нише под шторы

## Примечания

1. Разрезы — по линиям 1–1, 2–2 на плане потолков. Отметки — от ±0,000 чистого пола, м; размеры — мм.
2. Высоты мебели и дверных блоков за секущей плоскостью сверены с низом потолка над ними: верх ниже низа короба и поля.
3. ГКЛ 12,5 мм по каркасу П113; перепад уровней и бортик карниза — ГКЛ по ПП 60×27 (узел 1). Ниша под шторы — на всю длину стены с окном, карниз на закладной до обшивки (узел 2).
4. Толщины плит перекрытия и пирога пола показаны условно.

| | | | | | |
|---|---|---|---|---|---|
| | | | | | Проект: Дом 331 м² |
| | Лист | № док. | Подпись | Дата | Разрезы и узлы потолков |
| Дизайнер | Кырлан А.С. | | | 19.10.26 | |

| Стадия | Лист | Листов |
|---|---|---|
| П | 33 | 156 |

выпуск 18.10.2026 № 8cd922c868 · стр. 33 из 156

Правка к этому листу

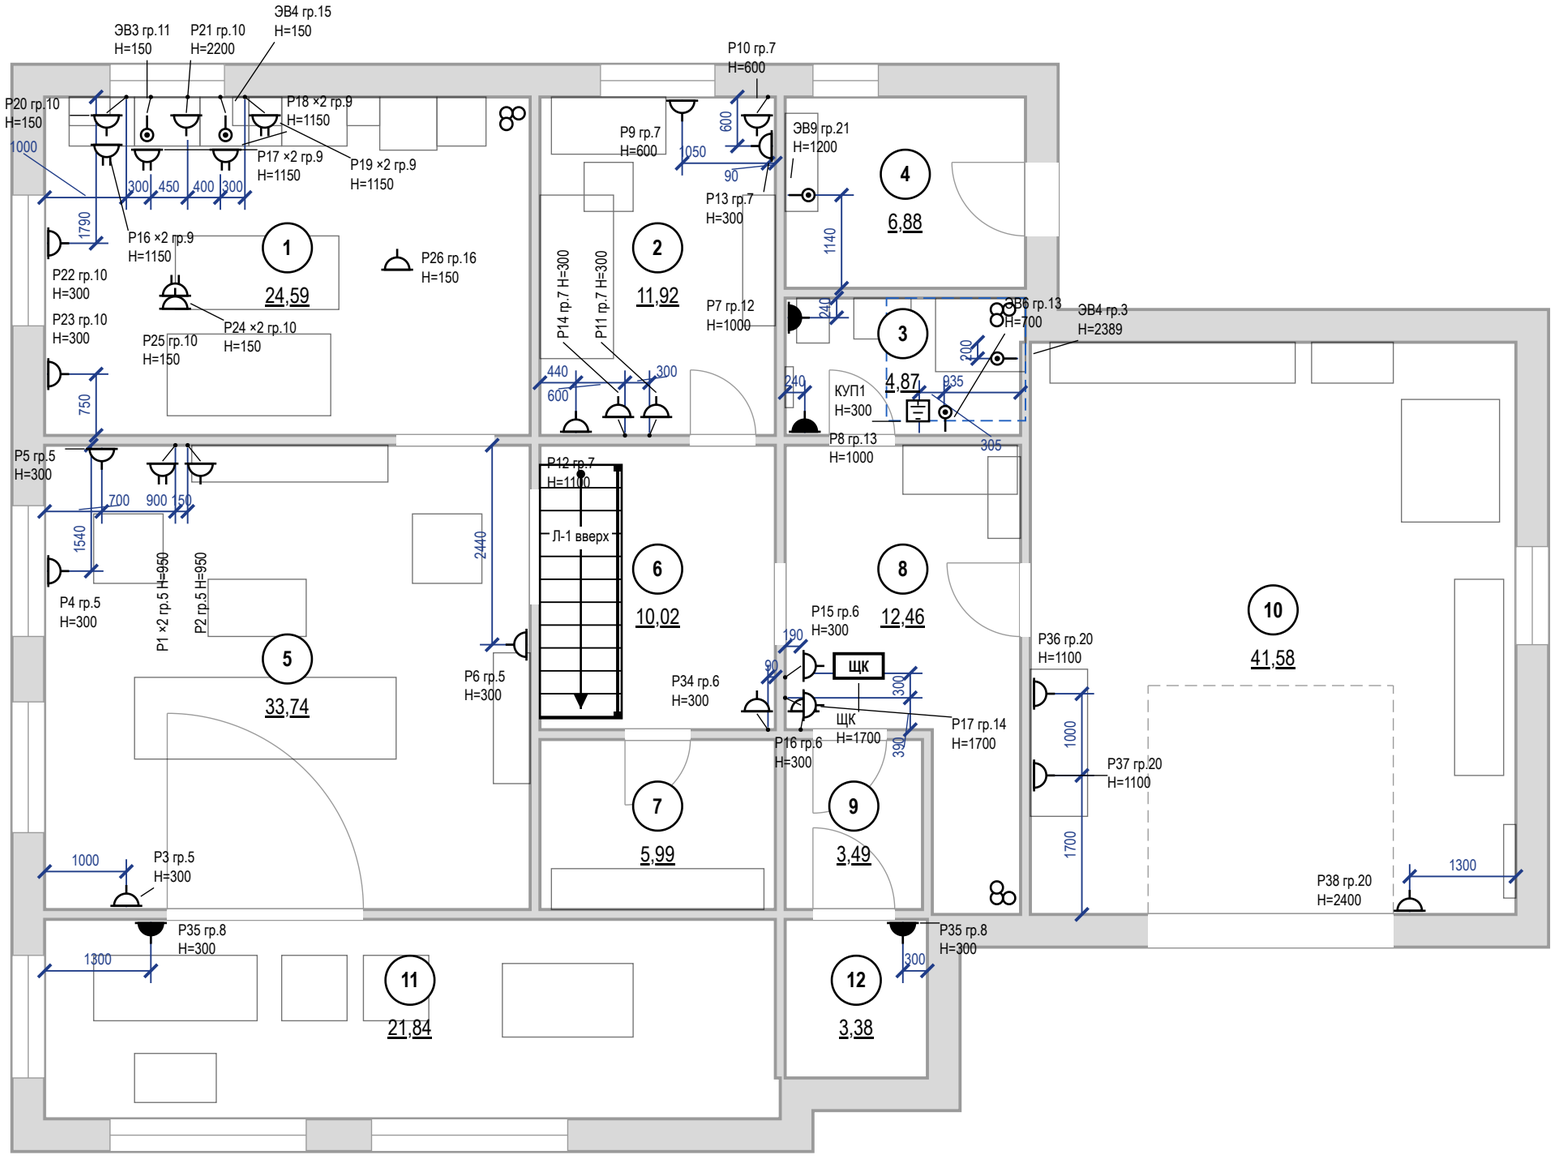


## Условные обозначения

- розетка с заземляющим контактом; у знака марка, ×N — постов в рамке, гр. — группа щита, H — высота оси, мм
- то же, рамка на 2 поста (число черточек — число постов)
- розетка влагозащищённая IP44
- вывод кабеля для подключения прибора (без розетки), марка ЭВ
- КУП — коробка уравнивания потенциалов (ДСУП), проводник к шине PE щита
- ЩК — щит квартирный
- знак разведён для читаемости: точка на стене у выноски, привязка — до неё
- граница зоны 2 ванной (600 мм от ванны/поддона)
- мебель и сантехприборы — подложка
- стояк: К1 — канализация, В1 — ХВС, Т3 — ГВС
- 1 — номер помещения, площадь м²

## Примечания

1. За отметку 0,000 принят уровень чистого пола. Высоты H — от чистого пола до оси изделия; привязки — от чистовой грани стены до оси механизма (у рамки на несколько постов — до оси рамки).
2. Высота установки, не указанная на плане: розетки — 300 мм от чистого пола; выводы кабеля — по паспорту прибора.
3. Розетки в санузле — только вне зон 0–2 (ПУЭ 7.1.48, ГОСТ Р 50571.7.701-2024), IP44, через УЗО 30 мА.
4. Розеточные и мокрые линии — через УЗО или дифавтомат с током утечки не более 30 мА (ПУЭ 7.1.79); в санузле выполнить ДСУП (ПУЭ 7.1.87–7.1.88).
5. Кабель — медный, исполнение нг(A)-LS (ГОСТ 31565-2012); скрытая прокладка только горизонтально и вертикально, фактические трассы зафиксировать исполнительной схемой до закрытия отделкой.
6. Расчёт нагрузок, токов КЗ, селективности и сечений — по проекту ЭОМ организации с допуском СРО; лист задаёт состав, расположение и группы.
7. Выводы кухонной техники — после утверждения проекта кухни (ориентировочно); привязки выводов даны от осей модулей гарнитура и пересматриваются вместе с проектом кухни.
8. Электрический тёплый пол проектом не предусмотрен; при решении заказчика устроить — отдельный лист «План тёплых полов»: контуры с отступом 100 мм от стен и мебели без ножек, датчик в гофре, терморегулятор, своя группа щита через УЗО 30 мА.
9. Ведомости электроточек, изделий, светильников и расшифровка клавиш — лист «Ведомость электроточек и изделий».

| | | | | | |
|---|---|---|---|---|---|
| | | | | | Проект: Дом 331 м² |
| | Лист | № док. | Подпись | Дата | |
| Дизайнер | Кырлан А.С. | | | 19.10.26 | План розеток и электровыводов · 1-й этаж |

| Стадия | Лист | Листов |
|---|---|---|
| П | 34 | 156 |

выпуск 18.10.2026 № 8cd922c868 · стр. 34 из 156

Правка к этому листу

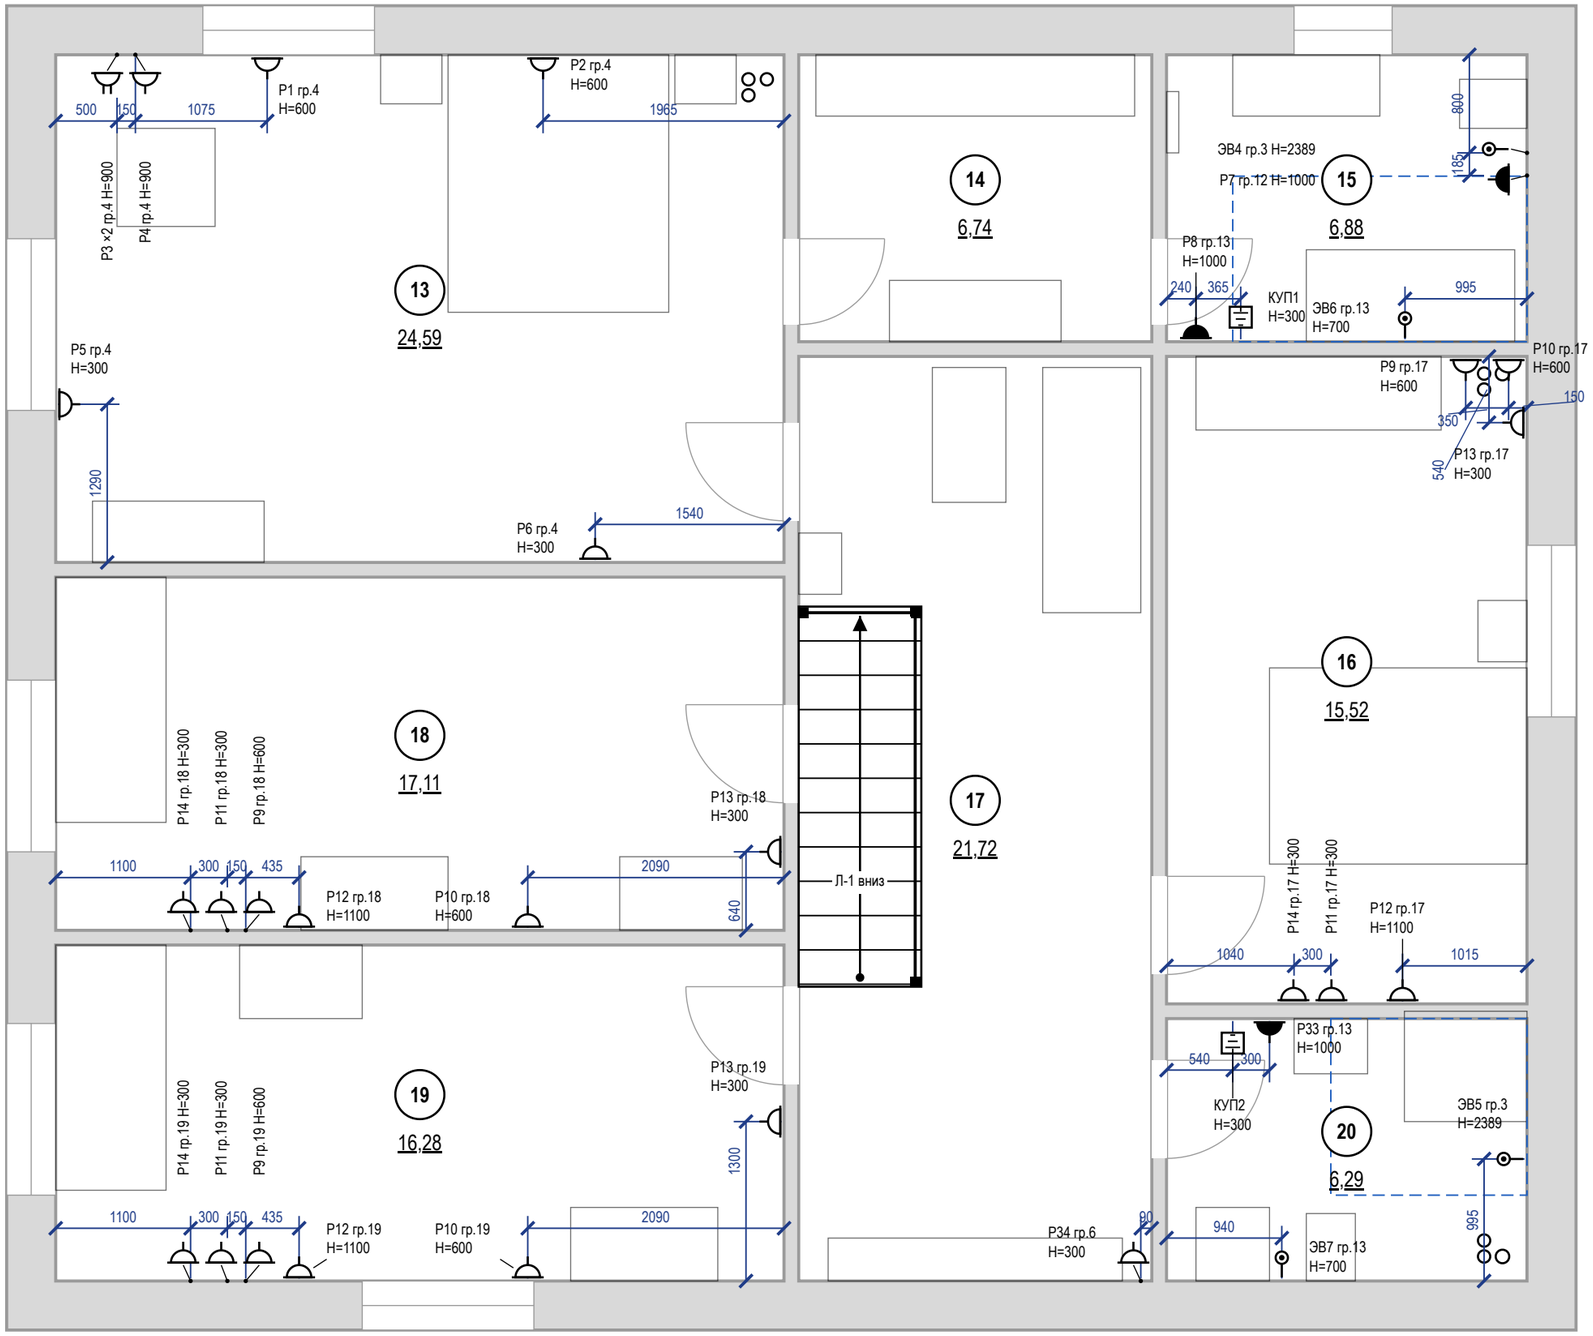


## Условные обозначения

- розетка с заземляющим контактом; у знака — марка, ×N постов в рамке, гр. — группа щита, H — высота оси, мм
- то же, рамка на 2 поста (число черточек — число постов)
- розетка влагозащищённая IP44
- вывод кабеля для подключения прибора (без розетки), марка ЭВ
- КУП — коробка уравнивания потенциалов (ДСУП), проводник к шине PE щита
- знак разведён для читаемости: точка на стене — у выноски, привязка — до неё
- граница зоны 2 ванной (600 мм от ванны/поддона)
- мебель и сантехприборы — подложка
- стояк: К1 — канализация, В1 — ХВС, Т3 — ГВС
- (1) номер помещения, площадь м²

## Примечания

1. За отметку 0,000 принят уровень чистого пола. Высоты H — от чистого пола до оси изделия; привязки — от чистовой грани стены до оси механизма (у рамки на несколько постов — до оси рамки).
2. Высота установки, не указанная на плане: розетки — 300 мм от чистого пола; выводы кабеля — по паспорту прибора.
3. Розетки в санузле — только вне зон 0–2 (ПУЭ 7.1.48, ГОСТ Р 50571.7.701-2024), IP44, через УЗО 30 мА.
4. Розеточные и мокрые линии — через УЗО или дифавтомат с током утечки не более 30 мА (ПУЭ 7.1.79); в санузле выполнить ДСУП (ПУЭ 7.1.87–7.1.88).
5. Кабель — медный, исполнение нг(А)-LS (ГОСТ 31565-2012); скрытая прокладка только горизонтально и вертикально, фактические трассы зафиксировать исполнительной схемой до закрытия отделкой.
6. Расчёт нагрузок, токов КЗ, селективности и сечений — по проекту ЭОМ организации с допуском СРО; лист задаёт состав, расположение и группы.
7. Электрический тёплый пол проектом не предусмотрен; при решении заказчика устроить — отдельный лист «План тёплых полов»: контуры с отступом 100 мм от стен и мебели без ножек, датчик в гофре, терморегулятор, своя группа щита через УЗО 30 мА.
8. Ведомости электроточек, изделий, светильников и расшифровка клавиш — лист «Ведомость электроточек и изделий».

| | | | | | |
|---|---|---|---|---|---|
| | Лист | № док. | Подпись | Дата | Проект: Дом 331 м² |
| Дизайнер | Кырлан А.С. | | | 19.10.26 | План розеток и электровыводов · Мансарда |

| Стадия | Лист | Листов |
|---|---|---|
| П | 35 | 156 |

выпуск 18.10.2026 № 8cd922c868 · стр. 35 из 156

Правка к этому листу

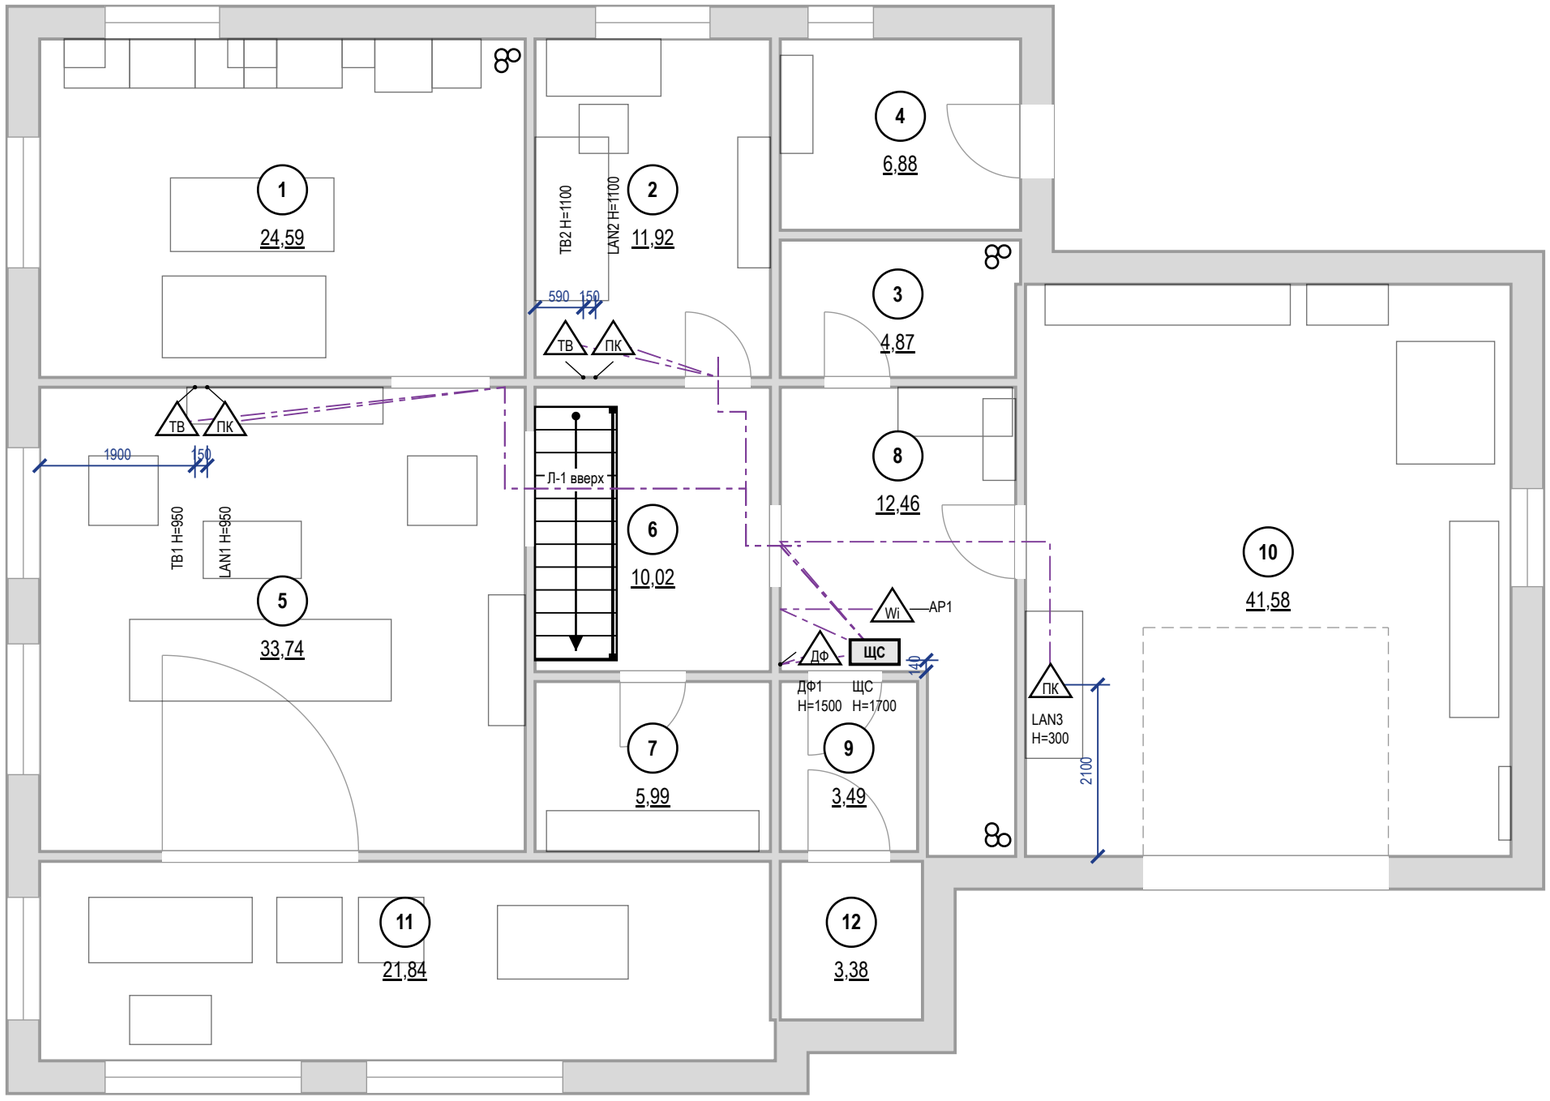


## Примечания

1. За отметку 0,000 принят уровень чистого пола. Высоты Н — от чистого пола до оси изделия; привязки — от чистовой грани стены до оси механизма (у рамки на несколько постов — до оси рамки).
2. Высота установки, не указанная на плане: розетки LAN и ТВ — 300 мм от чистого пола.
3. Слаботочные кабели — отдельно от силовых: в своей трубе или лотке, при параллельной прокладке не ближе 100 мм к силовым, пересечения под прямым углом; каждую точку — отдельным кабелем от ЩС без скруток.
4. Трассы на листе — принципиальные; фактические зафиксировать исполнительной схемой до закрытия отделкой. Силовые линии, УЗО 30 мА, ДСУП, кабель нг(А)-LS — по листам розеток и щита.
5. Проект силовой части и расчёт токов КЗ — по проекту ЭОМ; слаботочная часть согласуется с провайдером и управляющей компанией (домофон, коллективное ТВ).

| | | | | | |
|---|---|---|---|---|---|
| | | | | | Проект: Дом 331 м² |
| | Лист | № док. | Подпись | Дата | |
| Дизайнер | Кырлан А.С. | | | 19.10.26 | План слаботочных сетей · 1-й этаж |

| Стадия | Лист | Листов |
|---|---|---|
| П | 36 | 156 |

выпуск 18.10.2026 № 8cd922c868 · стр. 36 из 156

Правка к этому листу

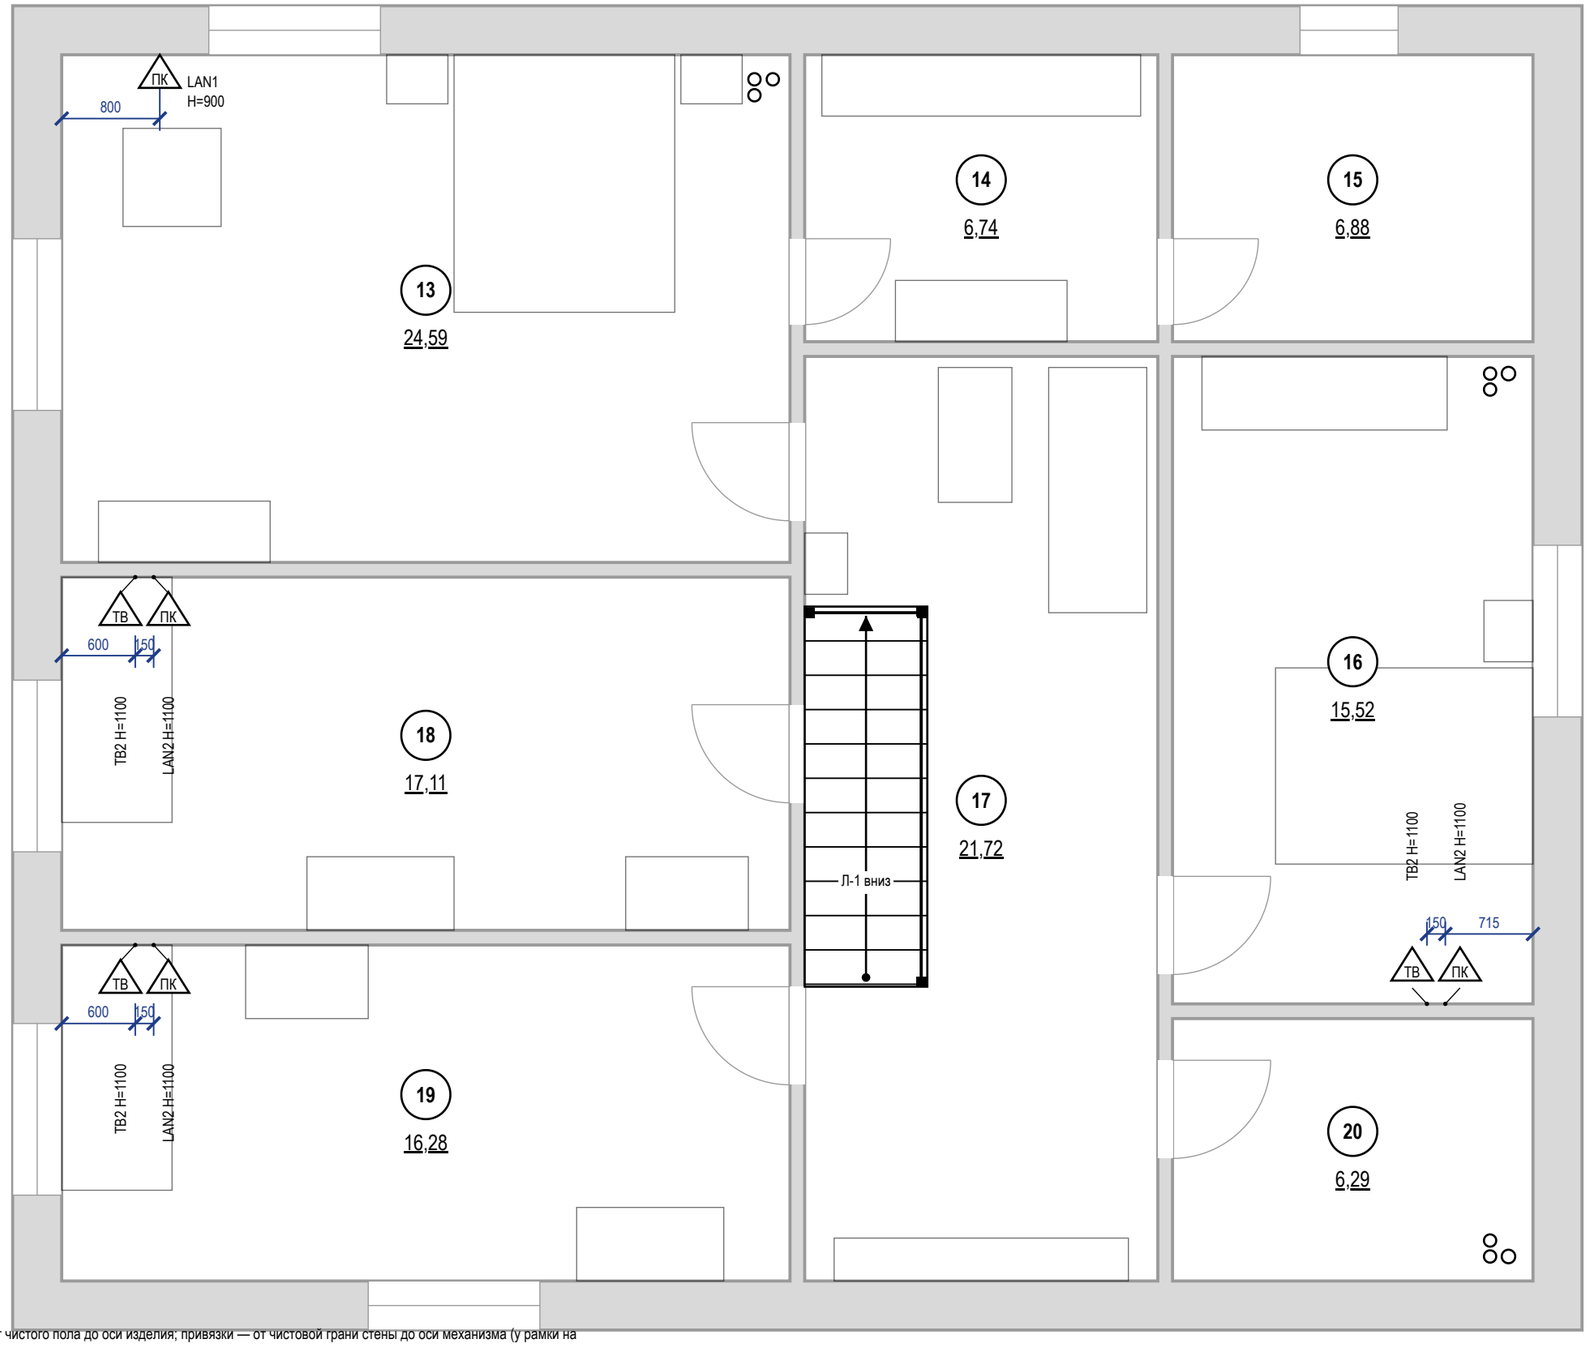


## Примечания

1. За отметку 0,000 принят уровень чистого пола. Высоты H — от чистого пола до оси изделия; привязки — от чистовой грани стены до оси механизма (у рамки на несколько постов — до оси рамки).
2. Высота установки, не указанная на плане: розетки LAN и ТВ — 300 мм от чистого пола.
3. Слаботочные кабели — отдельно от силовых: в своей трубе или лотке, при параллельной прокладке не ближе 100 мм к силовым, пересечения под прямым углом; каждую точку — отдельным кабелем от ЩС без скруток.
4. Трассы на листе — принципиальные; фактические зафиксировать исполнительной схемой до закрытия отделкой. Силовые линии, УЗО 30 мА, ДСУП, кабель нг(А)-LS — по листам розеток и щита.
5. Проект силовой части и расчёт токов КЗ — по проекту ЭОМ; слаботочная часть согласуется с провайдером и управляющей компанией (домофон, коллективное ТВ).

| | | | | | |
|---|---|---|---|---|---|
| | | | | | Проект: Дом 331 м² |
| | Лист | № док. | Подпись | Дата | |
| Дизайнер | Кырлан А.С. | | | 19.10.26 | План слаботочных сетей · Мансарда |

| Стадия | Лист | Листов |
|---|---|---|
| П | 37 | 156 |

выпуск 18.10.2026 № 8cd922c868 · стр. 37 из 156

Правка к этому листу

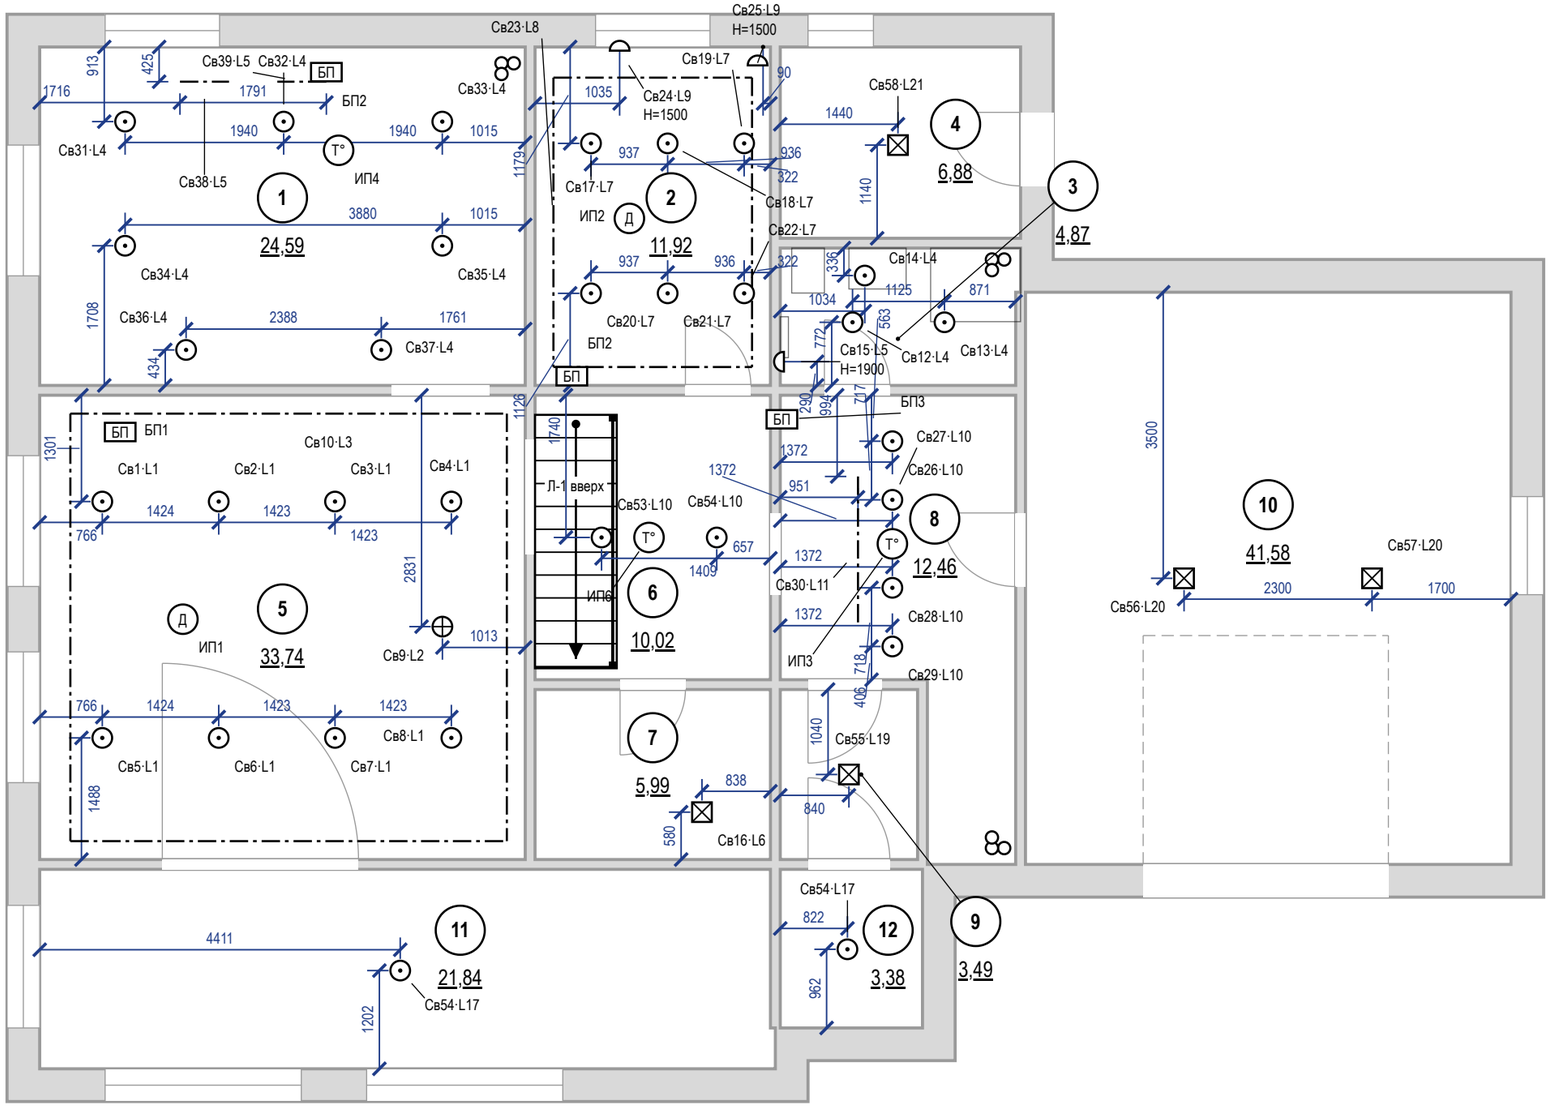


## Примечания

1. За отметку 0,000 принят уровень чистого пола. Высоты Н — от чистого пола до оси изделия; привязки — от чистовой грани стены до оси механизма (у рамки на несколько постов — до оси рамки).
2. Высота установки, не указанная на плане: светильники — на потолке; настенные — по отметке Н у знака. Привязки — до оси светильника от чистовой грани стены, по рядам.
3. Освещённость: Ен — СанПиН 1.2.3685-21, табл. 5.52 (на полу); Ф треб. = Ен·S/(U·MF) при U = 0,5 и MF = 0,71 (СП 52.13330.2016, табл. 4.3) — оценка, не светотехнический расчёт. Декоративная подсветка в Ф не входит.
4. Во влажных помещениях — светильники не ниже IP44; в зонах 0–2 ванной — по ГОСТ Р 50571.7.701-2024 (зона 1 — IPX5).
5. LED-лента в карнизе подсветки короба — по линии карниза с плана потолков; блок питания — в люке короба (БП на плане), питание ленты длиннее 5 м — с двух концов.
6. Розеточные и мокрые линии — через УЗО или дифавтомат с током утечки не более 30 мА (ПУЭ 7.1.79); в санузле выполнить ДСУП (ПУЭ 7.1.87–7.1.88).
7. Кабель — медный, исполнение нг(А)-LS (ГОСТ 31565-2012); скрытая прокладка только горизонтально и вертикально, фактические трассы зафиксировать исполнительной схемой до закрытия отделкой.
8. Расчёт нагрузок, токов КЗ, селективности и сечений — по проекту ЭОМ организации с допуском СРО; лист задаёт состав, расположение и группы.
9. Ведомость светильников — лист «Ведомость электроточек и изделий».

| | | | | | |
|---|---|---|---|---|---|
| | | | | | Проект: Дом 331 м² |
| | Лист | № док. | Подпись | Дата | План освещения · 1-й этаж |
| Дизайнер | Кырлан А.С. | | | 19.10.26 | Стадия: П; Лист: 38; Листов: 156 |

Правка к этому листу

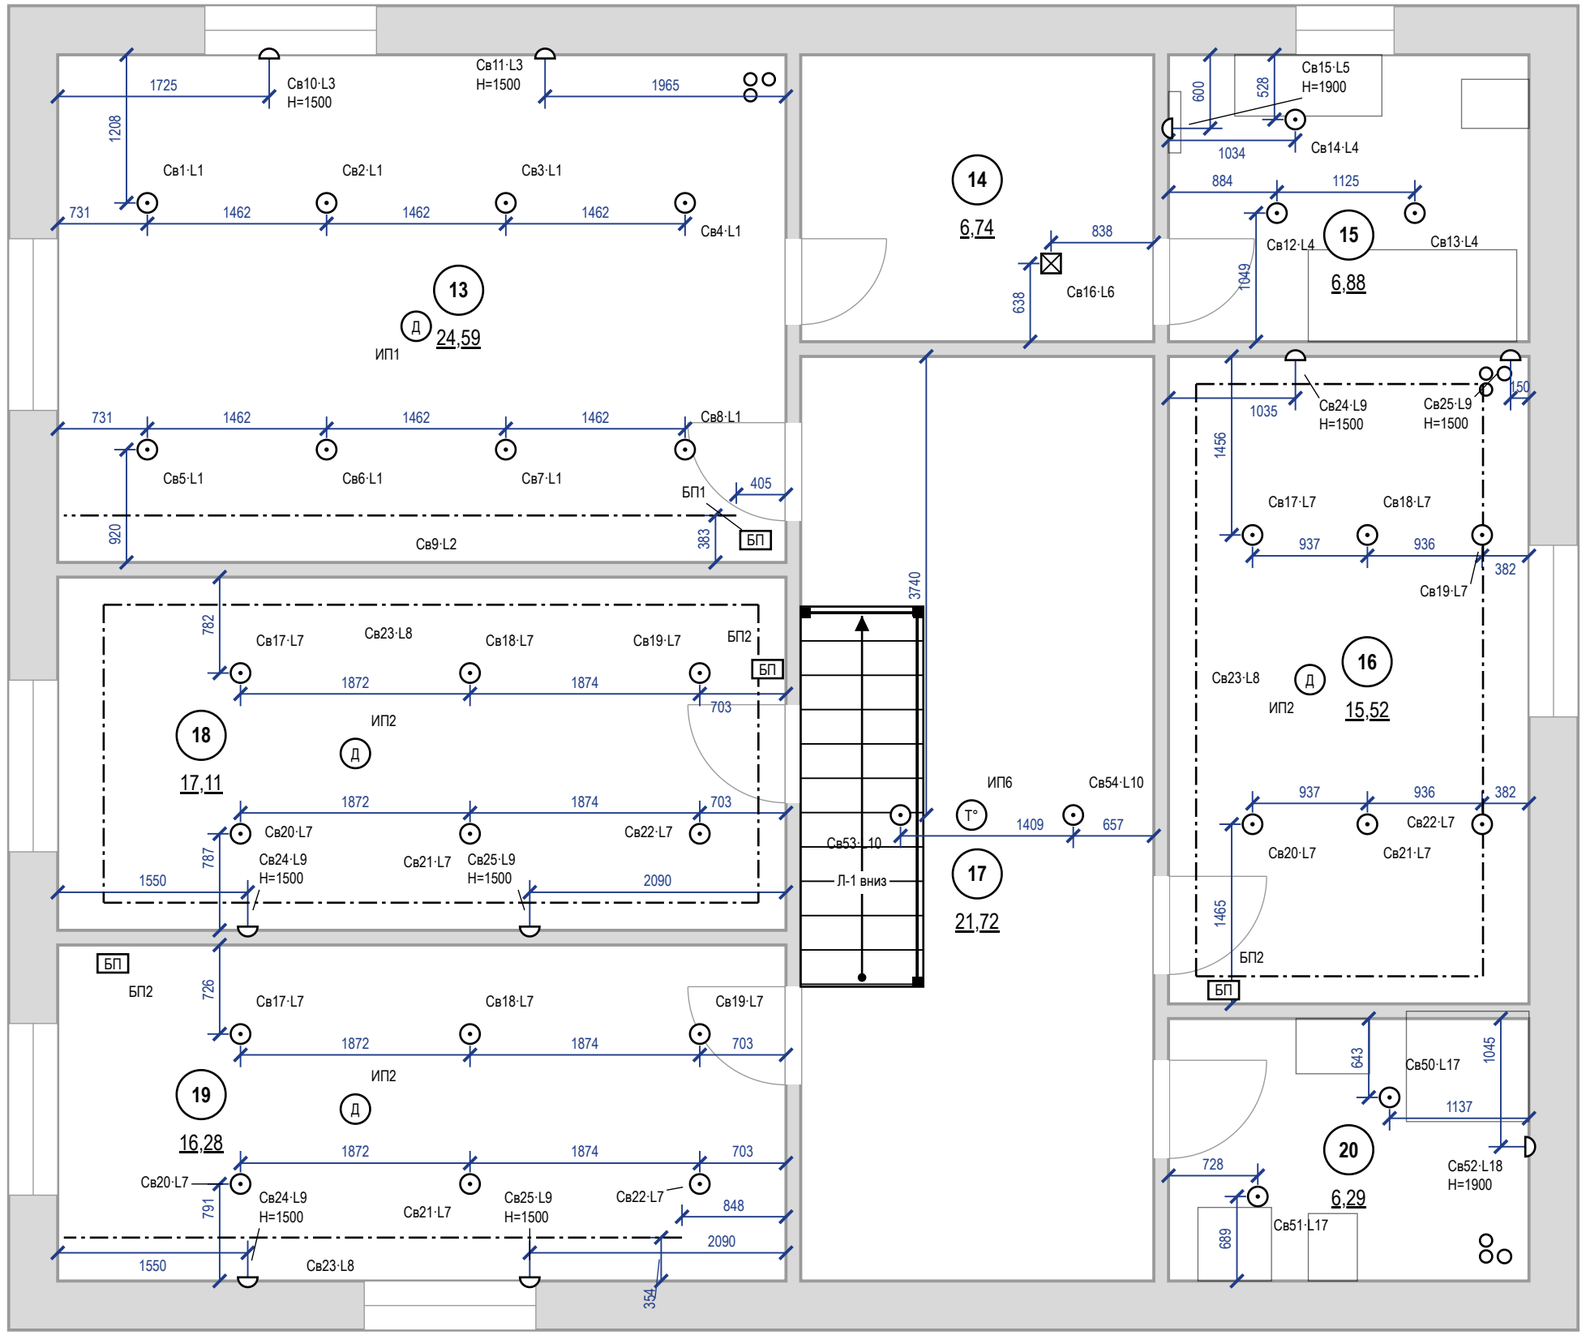


## Примечания

1. За отметку 0,000 принят уровень чистого пола. Высоты Н — от чистого пола до оси изделия; привязки — от чистовой грани стены до оси механизма (у рамки на несколько постов — до оси рамки).
2. Высота установки, не указанная на плане: светильники — на потолке; настенные — по отметке Н у знака. Привязки — до оси светильника от чистовой грани стены, по рядам.
3. Освещённость: Ен — СанПиН 1.2.3685-21, табл. 5.52 (на полу); Ф треб. = Ен·S/(U·MF) при U = 0,5 и MF = 0,71 (СП 52.13330.2016, табл. 4.3) — оценка, не светотехнический расчёт. Декоративная подсветка в Ф не входит.
4. Во влажных помещениях — светильники не ниже IP44; в зонах 0–2 ванной — по ГОСТ Р 50571.7.701-2024 (зона 1 — IPX5).
5. LED-лента в карнизе подсветки короба — по линии карниза с плана потолков; блок питания — в люке короба (БП на плане), питание ленты длиннее 5 м — с двух концов.
6. Розеточные и мокрые линии — через УЗО или дифавтомат с током утечки не более 30 мА (ПУЭ 7.1.79); в санузле выполнить ДСУП (ПУЭ 7.1.87–7.1.88).
7. Кабель — медный, исполнение нг(А)-LS (ГОСТ 31565-2012); скрытая прокладка только горизонтально и вертикально, фактические трассы зафиксировать исполнительной схемой до закрытия отделкой.
8. Расчёт нагрузок, токов КЗ, селективности и сечений — по проекту ЭОМ организации с допуском СРО; лист задаёт состав, расположение и группы.
9. Ведомость светильников — лист «Ведомость электроточек и изделий».

| | | | | |
|---|---|---|---|---|
| | Лист | № док. | Подпись | Дата |
| Дизайнер | Кырлан А.С. | | | 19.10.26 |

Проект: Дом 331 м²

План освещения · Мансарда

| Стадия | Лист | Листов |
|---|---|---|
| П | 39 | 156 |

выпуск 18.10.2026 № 8cd922c868 · стр. 39 из 156

Правка к этому листу

## Спецификация светильников

| Поз. | Марки | Наименование | Установка | Кол. | P, Вт | Σ P, Вт | Ф, лм | Тц, K | Ra | Угол, ° | IP | Дим. | Группа | Пом. |
|---|---|---|---|---|---|---|---|---|---|---|---|---|---|---|
| 1 | Св1–Св8, Св31–Св37 | Встраиваемый точечный | в ГКЛ, корпус ≤ 70 мм | 15 | 12 | 180 | 1000 | 3000 | 90 | — | 20 | — | L1, L4 | 1, 5 |
| 2 | Св38, Св39 | Линейный светильник | на поверхности | 1,2 м | 8 | 16 | 700 | 3000 | 90 | — | 20 | — | L5 | 1 |
| 3 | Св17–Св22 | Встраиваемый точечный | в ГКЛ, корпус ≤ 70 мм | 24 | 12 | 288 | 1050 | 2700 | 90 | — | 20 | — | L7 | 2, 16, 18, 19 |
| 4 | Св23 | Лента светодиодная 24 В | в карнизе короба, профиль с рассеивателем | 11,9 м | 9,6/м | 114,6 | 900/м | 2700 | 90 | — | 20 | да | L8 | 2 |
| 5 | Св10, Св11, Св24, Св25 | Настенный (бра) | на стене, H=1500 | 10 | 6 | 60 | 400 | 2700 | 90 | 60 | 20 | да | L3, L9 | 2, 13, 16, 18, 19 |
| 6 | Св12–Св14, Св51 | Встраиваемый точечный | в ГКЛ, корпус ≤ 70 мм | 7 | 6 | 42 | 500 | 3000 | 90 | — | 44 | — | L4, L17 | 3, 15, 20 |
| 7 | Св15, Св52 | Настенный светильник над зеркалом, драйвер встроен | над зеркалом, H=1900 | 3 | 8 | 24 | 600 | 3000 | 90 | — | 44 | — | L5, L18 | 3, 15, 20 |
| 8 | Св16, Св55, Св58 | Потолочный накладной | на потолке | 4 | 10 | 40 | 900 | 3000 | 90 | — | 20 | — | L6, L19, L21 | 4, 7, 9, 14 |
| 9 | Св9 | Подвесной | подвес, низ H=1600 | 1 | 15 | 15 | 1200 | 2700 | 90 | — | 20 | — | L2 | 5 |
| 10 | Св10 | Лента светодиодная 24 В | в карнизе короба, профиль с рассеивателем | 21,1 м | 9,6/м | 202,9 | 900/м | 2700 | 90 | — | 20 | да | L3 | 5 |
| 11 | Св26–Св29, Св53, Св54 | Встраиваемый точечный | в ГКЛ, корпус ≤ 70 мм | 8 | 7 | 56 | 600 | 3000 | 90 | — | 20 | — | L10 | 6, 8, 17 |
| 12 | Св30 | Лента светодиодная 24 В | в коробе, профиль с рассеивателем, датчик движения | 1,8 м | 4,8/м | 8,6 | 150/м | 2700 | 90 | — | 20 | нет | L11 | 8 |
| 13 | Св56, Св57 | Потолочный накладной | на потолке | 2 | 24 | 48 | 2500 | 3000 | 90 | — | 20 | — | L20 | 10 |
| 14 | Св54 | Встраиваемый точечный | встраиваемый | 2 | 9 | 18 | 800 | 3000 | 90 | — | 44 | — | L17 | 11, 12 |
| 15 | Св1–Св8 | Встраиваемый точечный | в ГКЛ, корпус ≤ 70 мм | 8 | 12 | 96 | 1000 | 2700 | 90 | — | 20 | — | L1 | 13 |
| 16 | Св9, Св23 | Лента светодиодная 24 В | в коробе, профиль с рассеивателем | 12 м | 9,6/м | 115,2 | 900/м | 2700 | 90 | — | 20 | да | L2, L8 | 13, 19 |
| 17 | Св23 | Лента светодиодная 24 В | в карнизе короба, профиль с рассеивателем | 14,3 м | 9,6/м | 137,7 | 900/м | 2700 | 90 | — | 20 | да | L8 | 16 |
| 18 | Св23 | Лента светодиодная 24 В | в карнизе короба, профиль с рассеивателем | 15,5 м | 9,6/м | 149,2 | 900/м | 2700 | 90 | — | 20 | да | L8 | 18 |
| 19 | Св50 | Встраиваемый точечный | в ГКЛ, корпус ≤ 70 мм | 1 | 7 | 7 | 600 | 3000 | 90 | — | 44 | — | L17 | 20 |
| | | **Итого** | | **85 шт + 78 м** | | **1618,3** | | | | | | | | |

## LED-ленты, линейные светильники и блоки питания

| Марка | Пом. | L, м | U, В | Вт/м | Σ P, Вт | БП | P БП, Вт | Загр., % | Питание | Доступ к БП |
|---|---|---|---|---|---|---|---|---|---|---|
| Св38 | 1 | 0,6 | 24 | — | 8 | БП2 | 200 | 238 | встроенный ввод | люк 300×300 в коробе У1 у окна |
| Св39 | 1 | 0,6 | 24 | — | 8 | БП2 | 200 | 238 | встроенный ввод | люк 300×300 в коробе У1 у окна |
| Св23 | 2 | 11,9 | 24 | 9,6 | 114,6 | БП2 | 200 | 238 | с двух концов | люк 300×300 в коробе У1 у окна |
| Св10 | 5 | 21,1 | 24 | 9,6 | 202,9 | БП1 | 200 | 130 | с двух концов | люк 300×300 в коробе У1 у входа |
| Св30 | 8 | 1,8 | 24 | 4,8 | 8,6 | БП3 | 20 | 43 | с одного конца | в шкафу М16, верхняя полка |
| Св9 | 13 | 6 | 24 | 9,6 | 57,6 | БП1 | 200 | 130 | с двух концов | люк 300×300 в коробе У1 у входа |
| Св23 | 16 | 14,3 | 24 | 9,6 | 137,7 | БП2 | 200 | 238 | с двух концов | люк 300×300 в коробе У1 у окна |
| Св23 | 18 | 15,5 | 24 | 9,6 | 149,2 | БП2 | 200 | 238 | с двух концов | люк 300×300 в коробе У1 у окна |
| Св23 | 19 | 6 | 24 | 9,6 | 57,6 | БП2 | 200 | 238 | с двух концов | люк 300×300 в коробе У1 у окна |

## Сценарии освещения

| Пом. | Сценарий | Группы и уровни, % | Чем включается |
|---|---|---|---|
| 2 | Вечер | L7 споты — 0; L8 подсветка короба — 100; L9 бра — 100 | S4, S5, S6 |
| 5 | Вечер | L1 общий свет (споты) — 0; L2 подвес над обеденным столом — 100; L3 лента в карнизе (диммер) — 50 | S1, S2, S2 светорегулятор, S3 |
| 5 | Гости | L1 общий свет (споты) — 100; L2 подвес над обеденным столом — 100; L3 лента в карнизе (диммер) — 100 | S1, S2, S2 светорегулятор, S3 |
| 5 | Кино | L1 общий свет (споты) — 0; L2 подвес над обеденным столом — 0; L3 лента в карнизе (диммер) — 20 | S2, S2 светорегулятор, S3 |
| 5 | Уборка | L1 общий свет (споты) — 100; L2 подвес над обеденным столом — 100; L3 лента в карнизе (диммер) — 0 | S1, S2, S3 |
| 13 | Вечер | L1 общий свет (споты) — 0; L2 подвес над обеденным столом — 100; L3 лента в карнизе (диммер) — 100 | S1, S2, S2 светорегулятор, S3 |
| 13 | Уборка | L1 общий свет (споты) — 100; L2 подвес над обеденным столом — 100; L3 лента в карнизе (диммер) — 0 | S1, S2, S3 |
| 16 | Вечер | L7 споты — 0; L8 подсветка короба — 100; L9 бра — 100 | S4, S5, S6 |
| 18 | Вечер | L7 споты — 0; L8 подсветка короба — 100; L9 бра — 100 | S4, S5, S6 |
| 19 | Вечер | L7 споты — 0; L8 подсветка короба — 100; L9 бра — 100 | S4, S5, S6 |

## Слои света

общий — равномерный свет помещения, по норме освещённости

рабочий — местный свет задачи: столешница, зеркало, чтение у кровати

акцентный — подсветка потолка, стен и ниш; не входит в поток общего света

ночной — путь спальня → санузел: не выше 2700 K, малая яркость, датчик движения

## Примечания

1. Позиции и марки Св — те же, что на плане освещения (лист «План освещения») и в ведомости светильников (лист «Ведомость электроточек и изделий»); группы L — по плану выключателей (лист «План выключателей»).
2. Модели светильников не назначены: подбор по графам спецификации — поток, Тц, Ra, угол, IP и диммирование не хуже указанных, мощность не больше; встраиваемые — под глубину короба (графа «Установка»). IP 20 — сухие помещения.
3. Длина LED-ленты в карнизе — по линии карниза плана потолков (лист «План потолков»); Σ P = Вт/м × длина. Блок питания загружен не больше чем на 80 %; лента 24 В длиннее 10 м питается с двух концов; доступ к блоку питания — люк ревизии 300×300 мм или место, указанное в таблице.
4. Сценарии: уровень — доля максимальной яркости группы, %; 0 — группа выключена. Уровень ниже 100 % — только у групп на светорегуляторе (задний фронт, ТЕ) с диммируемыми драйверами и блоками питания.
5. Мощность и поток — по паспортам принятых изделий, Σ P — установленная мощность освещения. Оценка освещённости — на плане освещения; это не светотехнический расчёт.
6. Не поместилось строк таблиц: 20 — продолжение выпустить отдельным листом.

| | | | | | | |
|---|---|---|---|---|---|---|
| | | | | | Проект: Дом 331 м² | |
| | Лист | № док. | Подпись | Дата | Спецификация светильников и сценарии освещения | Стадия / Лист / Листов |
| Дизайнер | Кырлан А.С. | | | 19.10.26 | | П / 40 / 156 |

выпуск 18.10.2026 № 8cd922c868 · стр. 40 из 156

Правка к этому листу

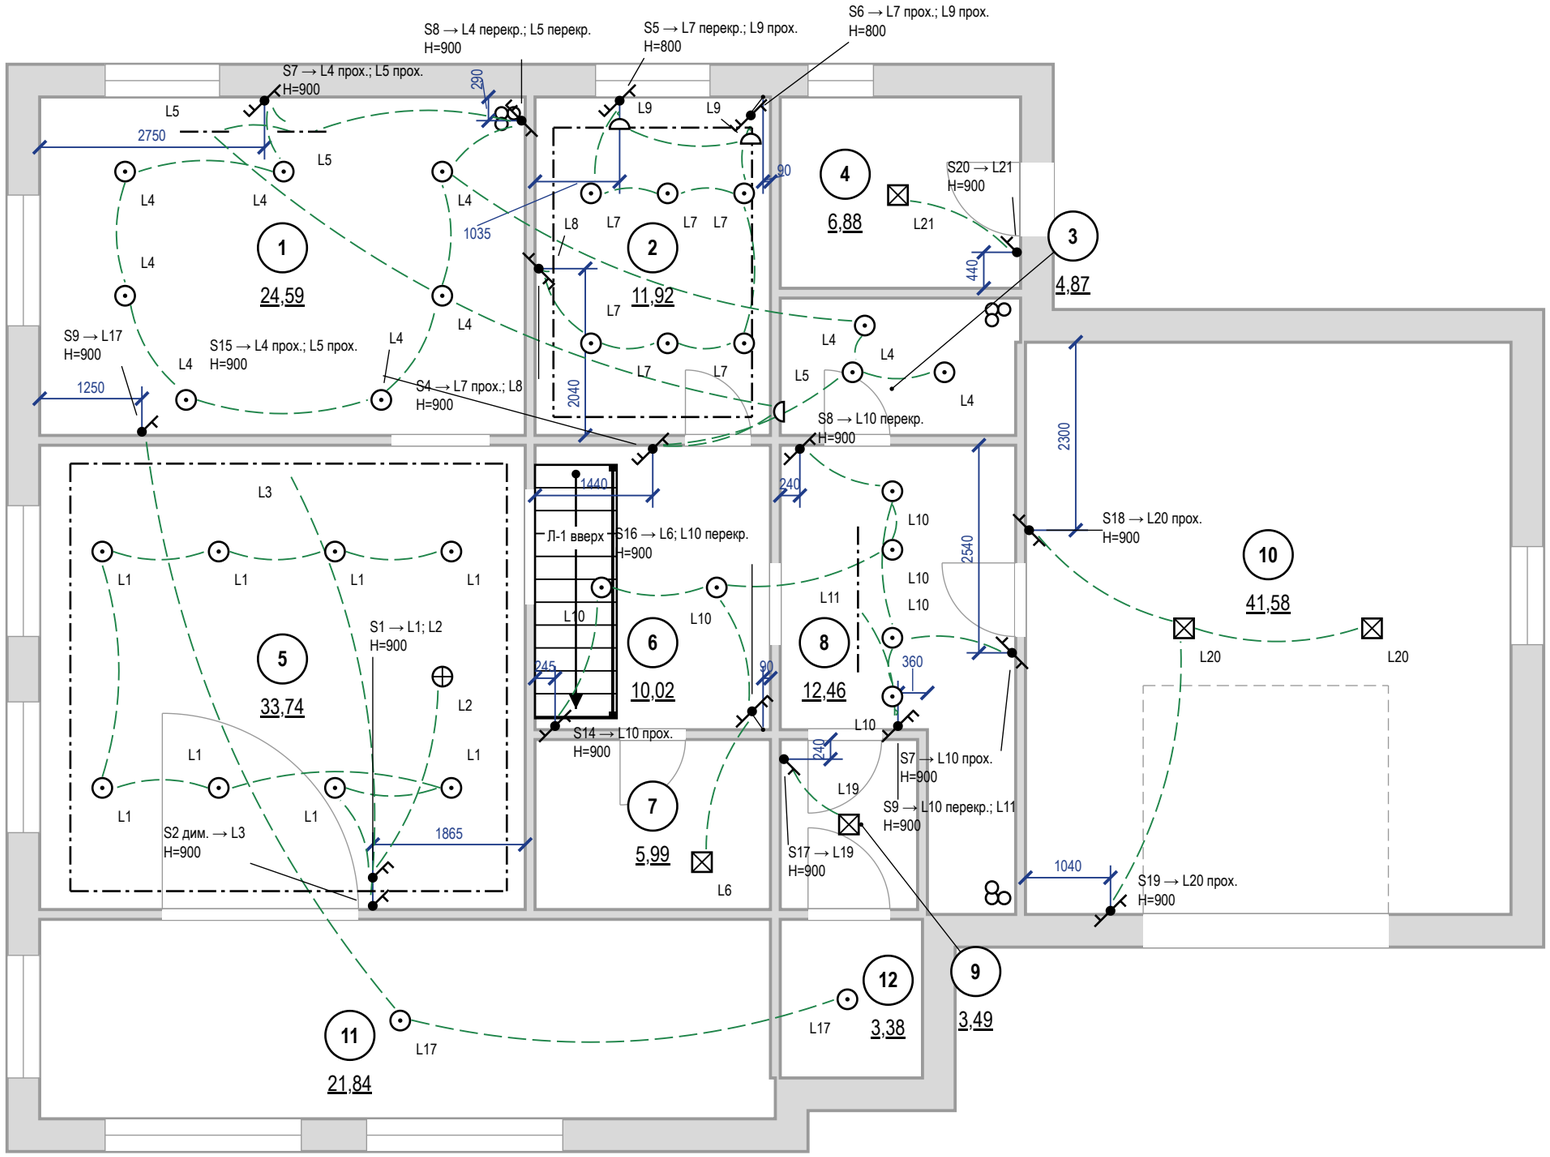


## Примечания

1. За отметку 0,000 принят уровень чистого пола. Высоты H — от чистого пола до оси изделия; привязки — от чистовой грани стены до оси механизма (у рамки на несколько постов — до оси рамки).
2. Высота установки, не указанная на плане: выключатели — 900 мм от чистого пола, со стороны дверной ручки (ПУЭ 7.1.51).
3. Линии связи показывают, какой выключатель какую группу L включает; это не трасса кабеля. Трасса — принципиальная, фактическую зафиксировать исполнительной схемой.
4. Группы из нескольких мест (L4 — S7, S8, S15; L5 — S7, S8, S15; L7 — S4, S5, S6; L9 — S5, S6; L10 — S7, S8, S9, S14, S16; L20 — S18, S19): на крайних местах проходные клавиши, на промежуточных — перекрёстные; механизмы — в ведомости изделий.
5. Светорегулятор — по заднему фронту (для LED-драйверов), совместимость с драйверами проверить до закупки.
6. Розеточные и мокрые линии — через УЗО или дифавтомат с током утечки не более 30 мА (ПУЭ 7.1.79); в санузле выполнить ДСУП (ПУЭ 7.1.87–7.1.88).
7. Кабель — медный, исполнение нг(A)-LS (ГОСТ 31565-2012); скрытая прокладка только горизонтально и вертикально, фактические трассы зафиксировать исполнительной схемой до закрытия отделкой.
8. Расчёт нагрузок, токов КЗ, селективности и сечений — по проекту ЭОМ организации с допуском СРО; лист задаёт состав, расположение и группы.
9. Расшифровка клавиш и ведомость изделий — лист «Ведомость электроточек и изделий».

| | | | | | |
|---|---|---|---|---|---|
| | | | | | Проект: Дом 331 м² |
| | Лист | № док. | Подпись | Дата | Управление светильниками · 1-й этаж |
| Дизайнер | Кырлан А.С. | | | 19.10.26 | |

| Стадия | Лист | Листов |
|---|---|---|
| П | 41 | 156 |

Правка к этому листу

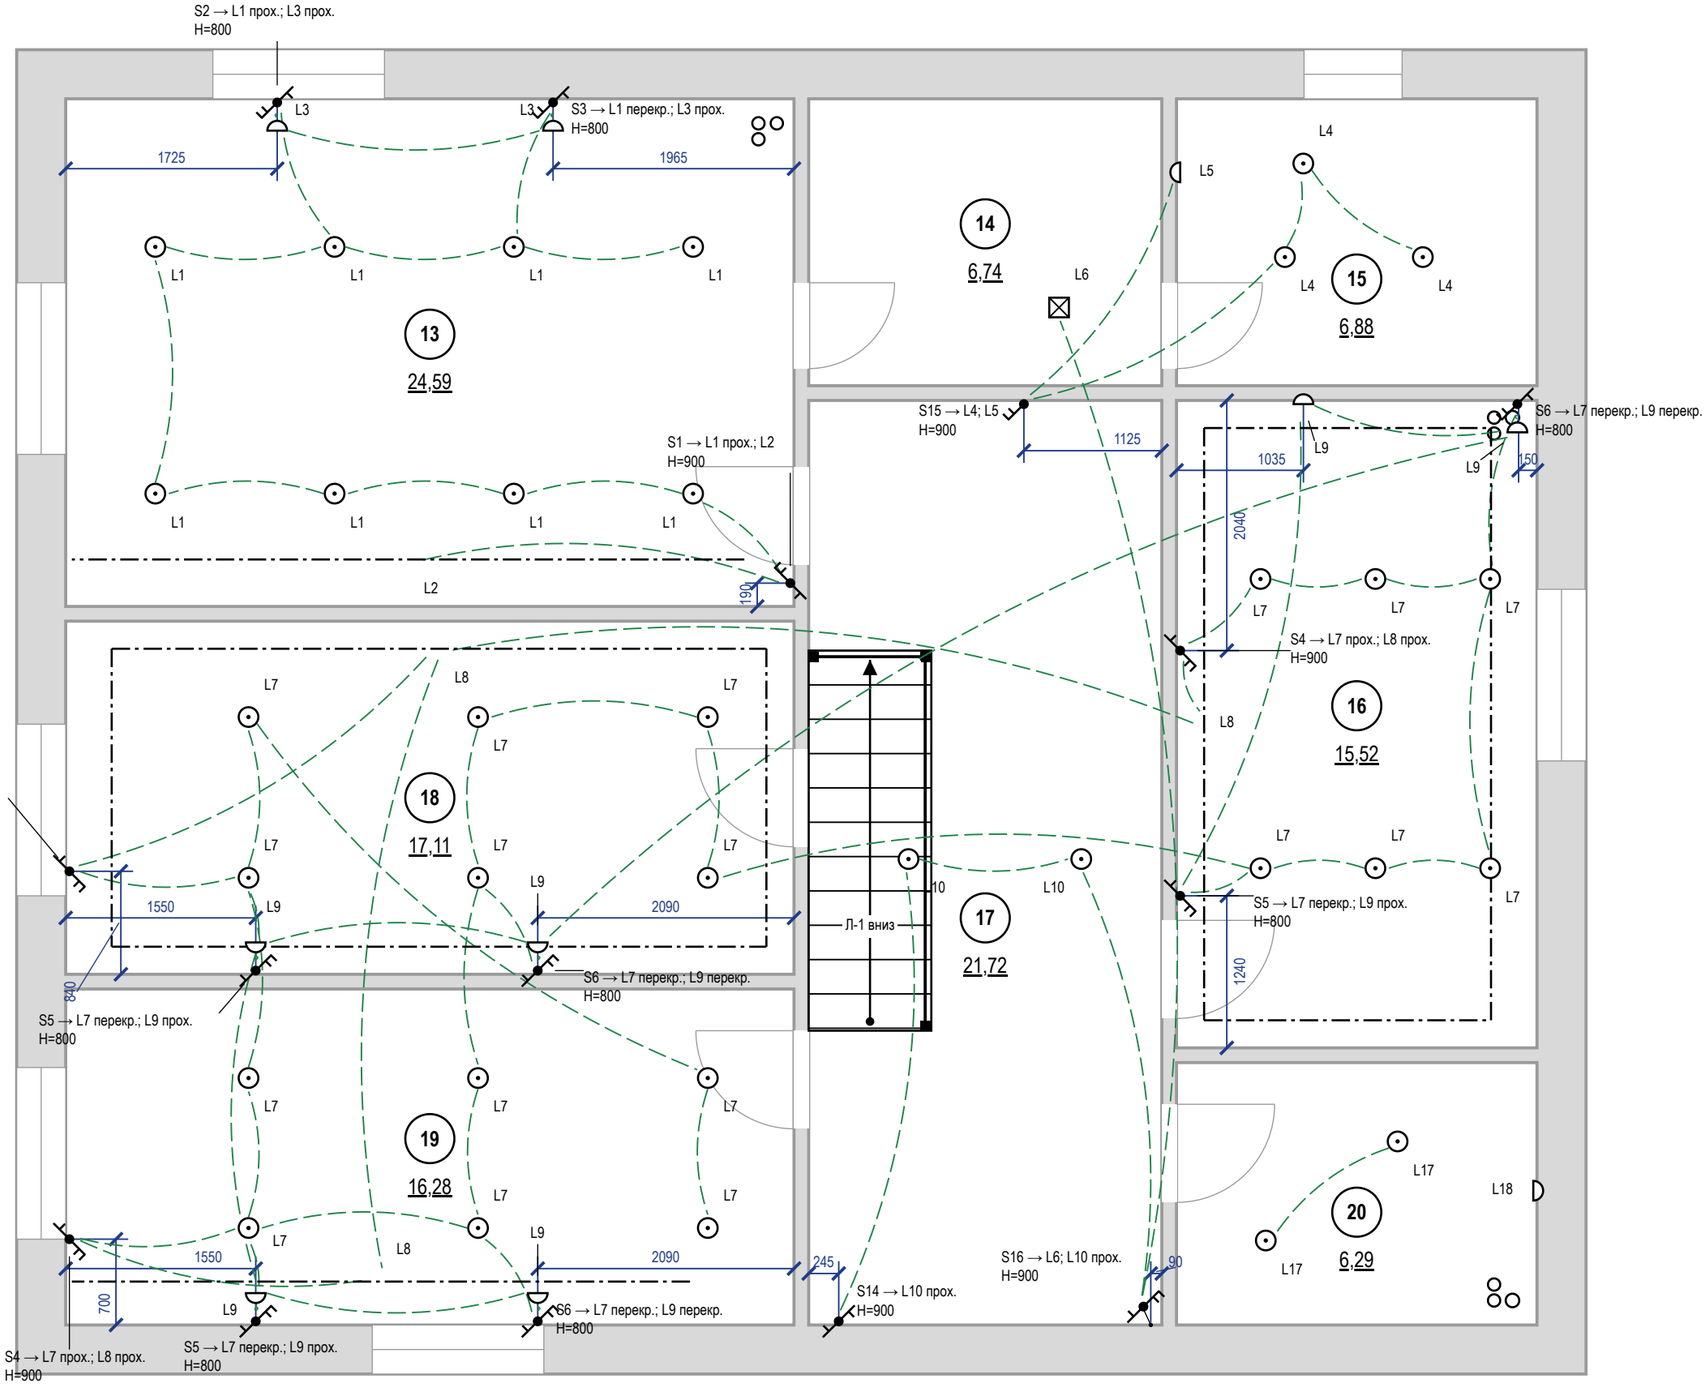


S4 → L7 прох.; L8 прох.
H=900

## Примечания

1. За отметку 0,000 принят уровень чистого пола. Высоты H — от чистого пола до оси изделия; привязки — от чистовой грани стены до оси механизма (у рамки на несколько постов — до оси рамки).
2. Высота установки, не указанная на плане: выключатели — 900 мм от чистого пола, со стороны дверной ручки (ПУЭ 7.1.51).
3. Линии связи показывают, какой выключатель какую группу L включает; это не трасса кабеля. Трасса — принципиальная, фактическую зафиксировать исполнительной схемой.
4. Группы из нескольких мест (L1 — S1, S2, S3; L3 — S2, S3; L7 — S4, S4, S4, S5, S5, S5, S6, S6, S6; L8 — S4, S4, S4; L9 — S5, S5, S5, S6, S6, S6; L10 — S14, S16): на крайних местах проходные клавиши, на промежуточных перекрёстные; механизмы — в ведомости изделий.
5. Розеточные и мокрые линии — через УЗО или дифавтомат с током утечки не более 30 мА (ПУЭ 7.1.79); в санузле выполнить ДСУП (ПУЭ 7.1.87–7.1.88).
6. Кабель — медный, исполнение нг(A)-LS (ГОСТ 31565-2012); скрытая прокладка только горизонтально и вертикально, фактические трассы зафиксировать исполнительной схемой до закрытия отделкой.
7. Расчёт нагрузок, токов КЗ, селективности и сечений — по проекту ЭОМ организации с допуском СРО; лист задаёт состав, расположение и группы.
8. Группы без выключателя: L17, L18 — назначить управление до монтажа.
9. Расшифровка клавиш и ведомость изделий — лист «Ведомость электроточек и изделий».

| | | | | | |
|---|---|---|---|---|---|
| | | | | | Проект: Дом 331 м² |
| | Лист | № док. | Подпись | Дата | Управление светильниками · Мансарда |
| Дизайнер | Кырлан А.С. | | | 19.10.26 | |

| Стадия | Лист | Листов |
|---|---|---|
| П | 42 | 156 |

выпуск 18.10.2026 № 8cd922c868 · стр. 42 из 156

Правка к этому листу

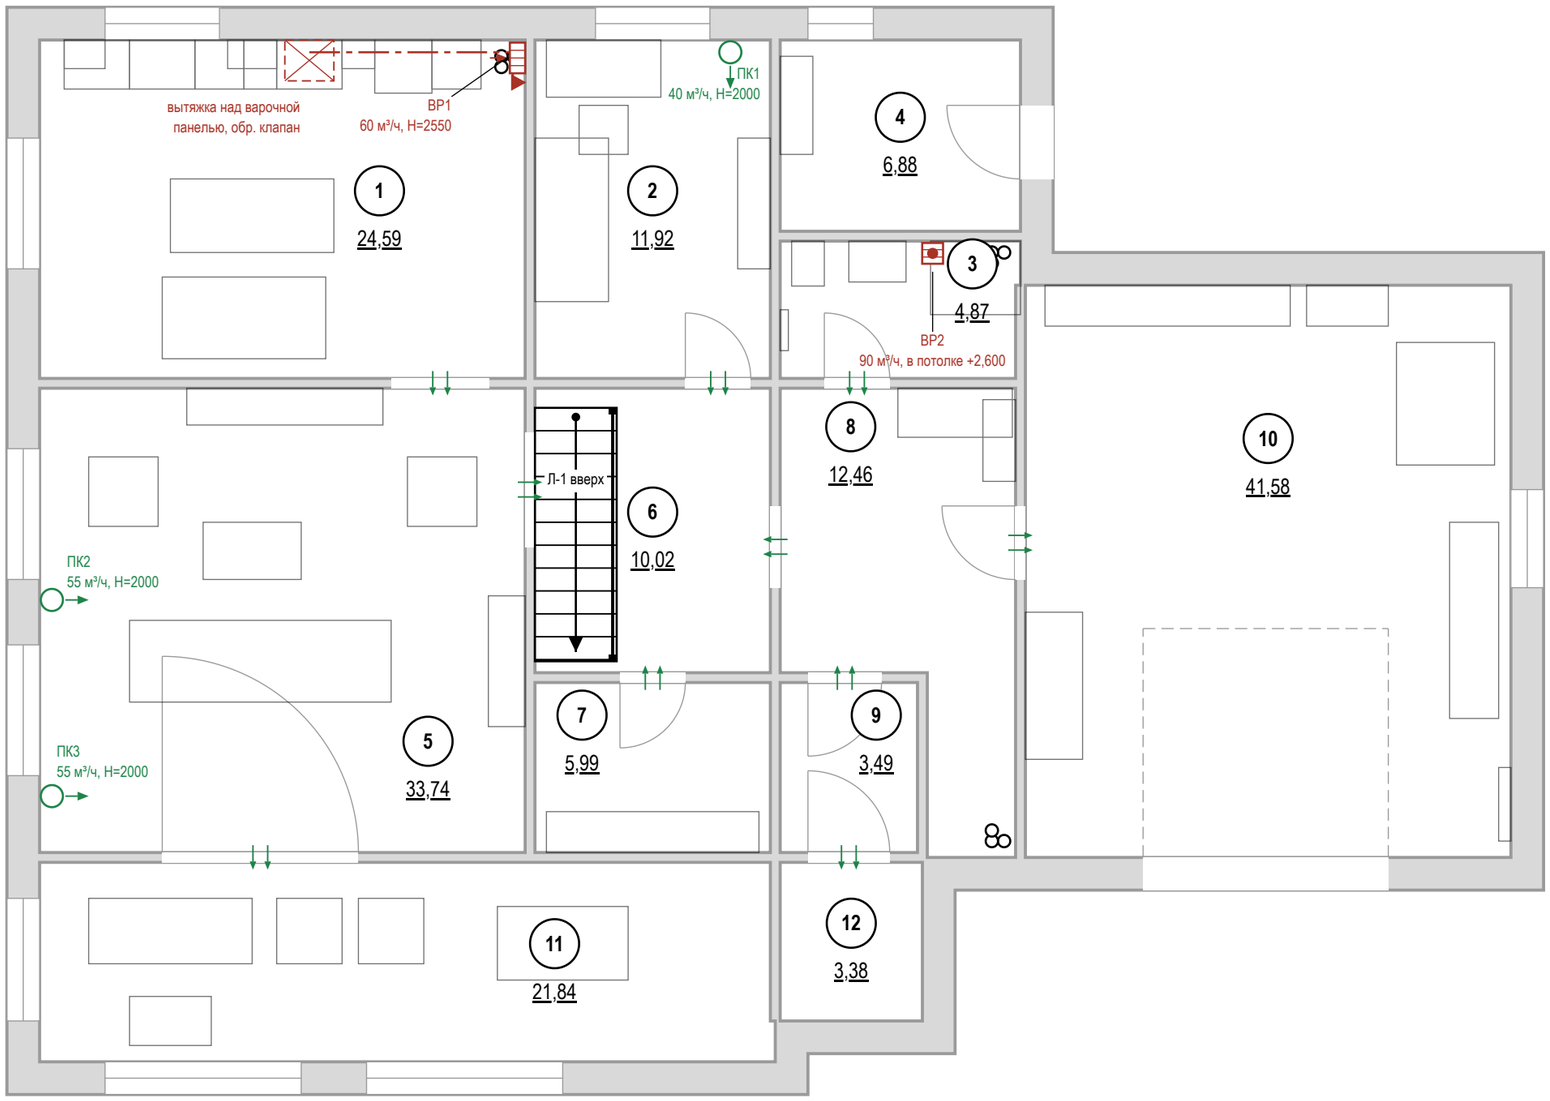


## Условные обозначения

- стояк: К1 — канализация, В1 — ХВС, Т3 ГВС
- 1 — номер помещения, площадь м²
- вытяжная решётка в вентканал: марка, расход м³/ч, Н центра от чистого пола
- вентилятор с обратным клапаном в подшивном потолке, воздуховод за потолком до канала
- приточный клапан (КИВ) в наружной стене: марка, расход, Н центра
- переток: зазор под полотном или переточная решётка
- кухонная вытяжка над варочной панелью
- воздуховод кухонной вытяжки в коробе под потолком
- отдельный вход воздуховода в вентканал, обратный клапан

## Воздухообмен, м³/ч

| № | Помещение | Выт. норма | Выт. проект | Прит. норма | Прит. проект | Устройства |
|---|---|---|---|---|---|---|
| 1 | Кухня-столовая | 60 | 60 | | | ВР1 |
| 2 | Кабинет-гостевая | | | 36 | 40 | ПК1 |
| 3 | Санузел 1 этажа | 50 | 90 | | | ВР2 |
| 4 | Котельная | 4 | | | | переток |
| 5 | Гостиная | | | 102 | 110 | ПК2, ПК3 |
| 7 | Кладовая | 3 | | | | переток |
| 10 | Гараж | 23 | | | | переток |
| | **Итого** | **140** | **150** | **120** | **150** | |

Воздухообмен квартиры — по большей из сумм притока и вытяжки: норма 140 м³/ч, проект 150 м³/ч.
Вытяжка не меньше притока — баланс сведён.

## Примечания

1. Расчёт систем ОВ и подбор оборудования — проектная организация с допуском СРО; лист даёт места, трассы и привязки.
2. Нормы вытяжки — СП 54.13330.2022 (Изм. 1, 2), табл. 7.1: кухня с электроплитой 60 м³/ч, с газовой 100; ванная и совмещённый санузел 50; уборная 25; гардеробная 0,2 ч⁻¹. Приток в жилые — 3 м³/ч на 1 м² (менее 20 м² общей площади на человека), иначе 30 м³/ч на человека.
3. Вентканалы и шахты не сужать, не переносить и не закрывать; вентилятор и кухонная вытяжка — через обратный клапан, без перекрытия естественной тяги.
4. Проектные расходы — не ниже нормы, вытяжка сведена с притоком вентиляторами мокрых помещений. Клапаны — в простенке у окна, центр 2000 мм, не над кроватью, не ближе 300 мм к стоякам отопления; типоразмер — на расход.
5. Под подшивным потолком вытяжка — в потолке, воздуховодом за потолком до канала. Кухонная вытяжка в воздухообмен не включена: воздуховод не менее Ø125 в коробе, вход в канал отдельный.
6. Переток — зазор под полотнами межкомнатных дверей или переточная решётка.
7. Кондиционирование заданием не предусмотрено; при установке трассы фреона и дренажа (не менее 40 мм/м, в К1 через сифон) и питание заложить до черновых работ.
8. Привязки оборудования — по паспортам приобретённых моделей, до черновых работ.

| | | | | | |
|---|---|---|---|---|---|
| | | | | | Проект: Дом 331 м² |
| | Лист | № док. | Подпись | Дата | |
| Дизайнер | Кырлан А.С. | | | 19.10.26 | План вентиляции · 1-й этаж |

| Стадия | Лист | Листов |
|---|---|---|
| П | 43 | 156 |

выпуск 18.10.2026 № 8cd922c868 · стр. 43 из 156

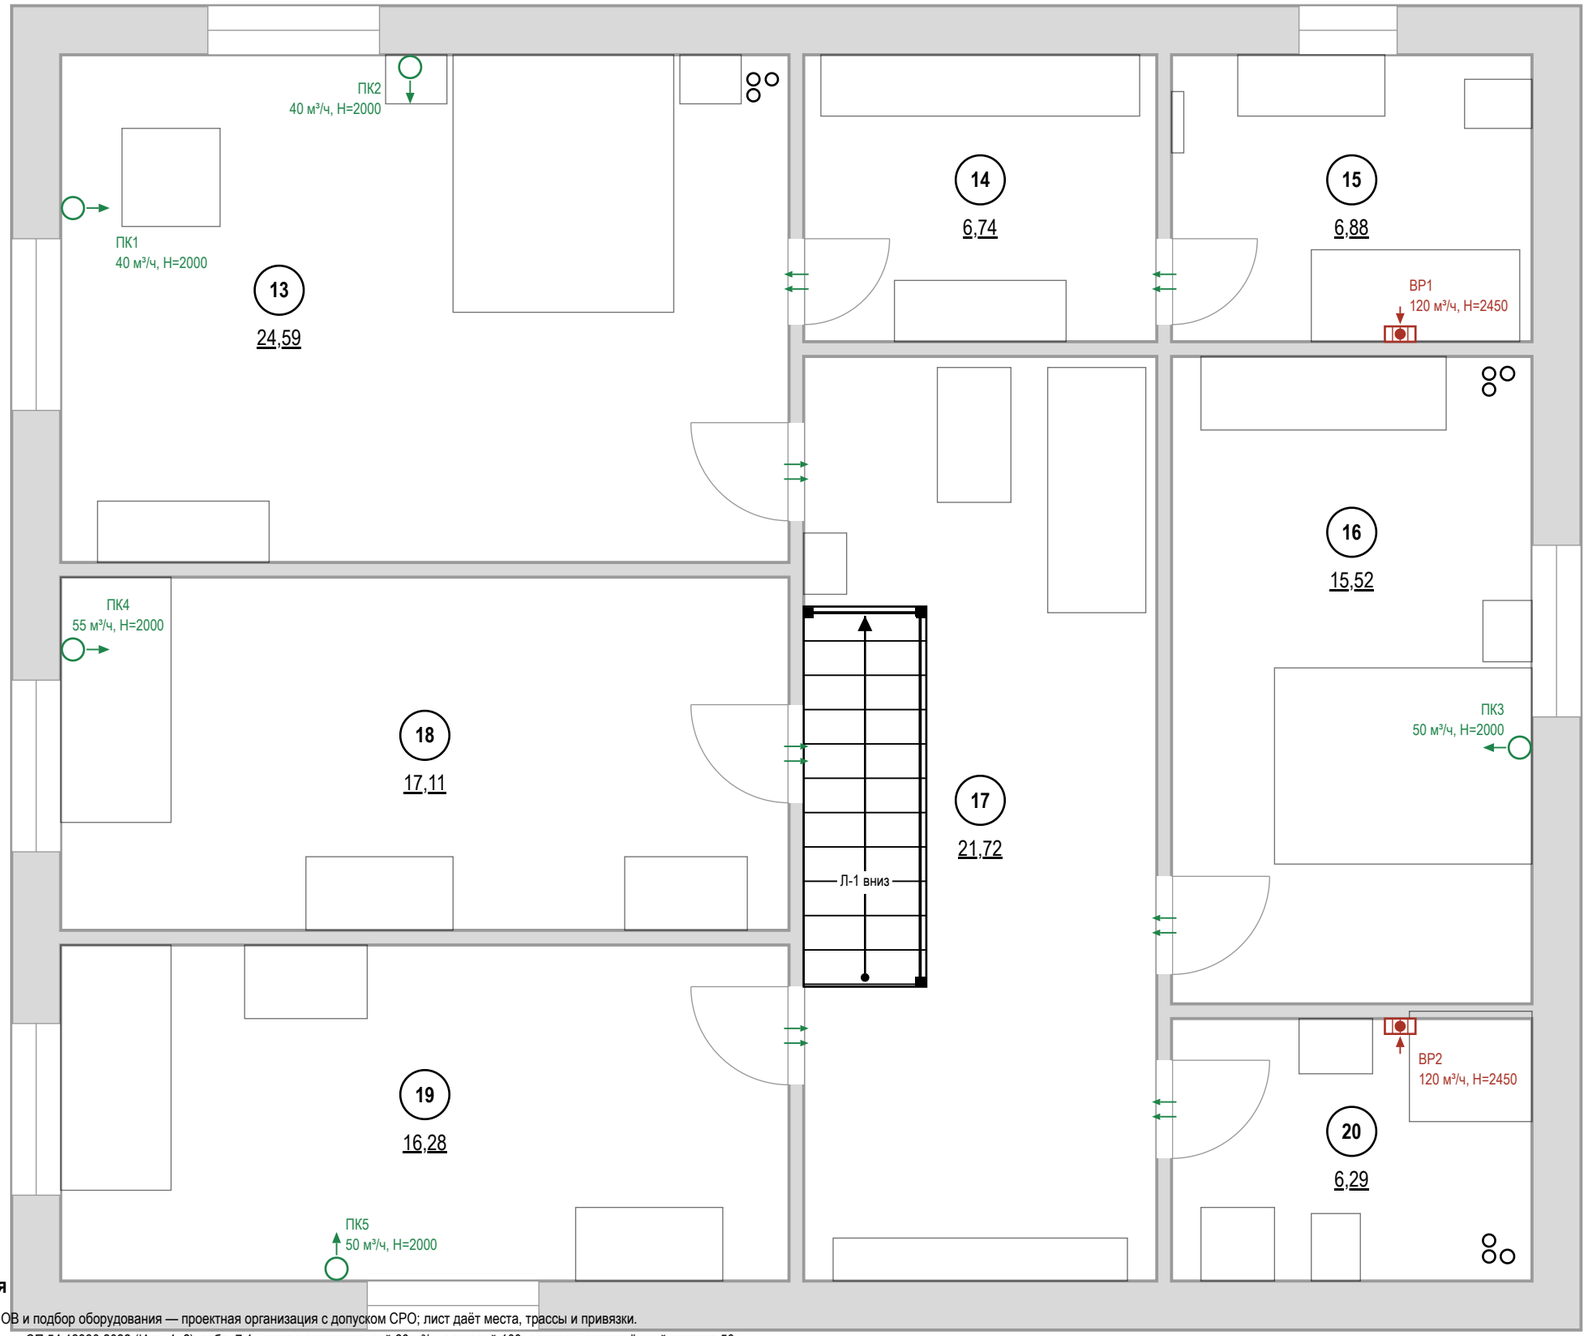


## Условные обозначения

- стояк: К1 — канализация, В1 — ХВС, Т3 — ГВС
- 1 — номер помещения, площадь м²
- вытяжная решётка с бытовым вентилятором и обратным клапаном: марка, расход, Н
- приточный клапан (КИВ) в наружной стене: марка, расход, Н центра
- переток: зазор под полотном или переточная решётка

## Воздухообмен, м³/ч

| № | Помещение | Выт. норма | Выт. проект | Прит. норма | Прит. проект | Устройства |
|---|---|---|---|---|---|---|
| 13 | Спальня мастер | | | 74 | 80 | ПК1, ПК2 |
| 14 | Гардеробная мастер | 4 | | | | переток |
| 15 | Санузел мастер | 50 | 120 | | | ВР1 |
| 16 | Спальня 2 | | | 47 | 50 | ПК3 |
| 18 | Спальня 3 | | | 52 | 55 | ПК4 |
| 19 | Спальня 4 | | | 49 | 50 | ПК5 |
| 20 | Санузел 2 | 50 | 120 | | | ВР2 |
| | **Итого** | **104** | **240** | **120** | **235** | |

Воздухообмен квартиры — по большей из сумм притока и вытяжки: норма 120 м³/ч, проект 240 м³/ч.
Вытяжка не меньше притока — баланс сведён.

## Примечания

1. Расчёт систем ОВ и подбор оборудования — проектная организация с допуском СРО; лист даёт места, трассы и привязки.
2. Нормы вытяжки — СП 54.13330.2022 (Изм. 1, 2), табл. 7.1: кухня с электроплитой 60 м³/ч, с газовой 100; ванная и совмещённый санузел 50; уборная 25; гардеробная 0,2 ч⁻¹. Приток в жилые — 3 м³/ч на 1 м² (менее 20 м² общей площади на человека), иначе 30 м³/ч на человека.
3. Вентканалы и шахты не сужать, не переносить и не закрывать; вентилятор и кухонная вытяжка — через обратный клапан, без перекрытия естественной тяги.
4. Проектные расходы — не ниже нормы, вытяжка сведена с притоком вентиляторами мокрых помещений. Клапаны — в простенке у окна, центр 2000 мм, не над кроватью, не ближе 300 мм к стоякам отопления; типоразмер — на расход.
5. Переток — зазор под полотнами межкомнатных дверей или переточная решётка.
6. Кондиционирование заданием не предусмотрено; при установке трассы фреона и дренажа (не менее 40 мм/м, в К1 через сифон) и питание заложить до черновых работ.
7. Привязки оборудования — по паспортам приобретённых моделей, до черновых работ.

| | Лист | № док. | Подпись | Дата |
|---|---|---|---|---|
| Дизайнер | Кырлан А.С. | | | 19.10.26 |

Проект: Дом 331 м²

План вентиляции · Мансарда

| Стадия | Лист | Листов |
|---|---|---|
| П | 44 | 156 |

Правка к этому листу

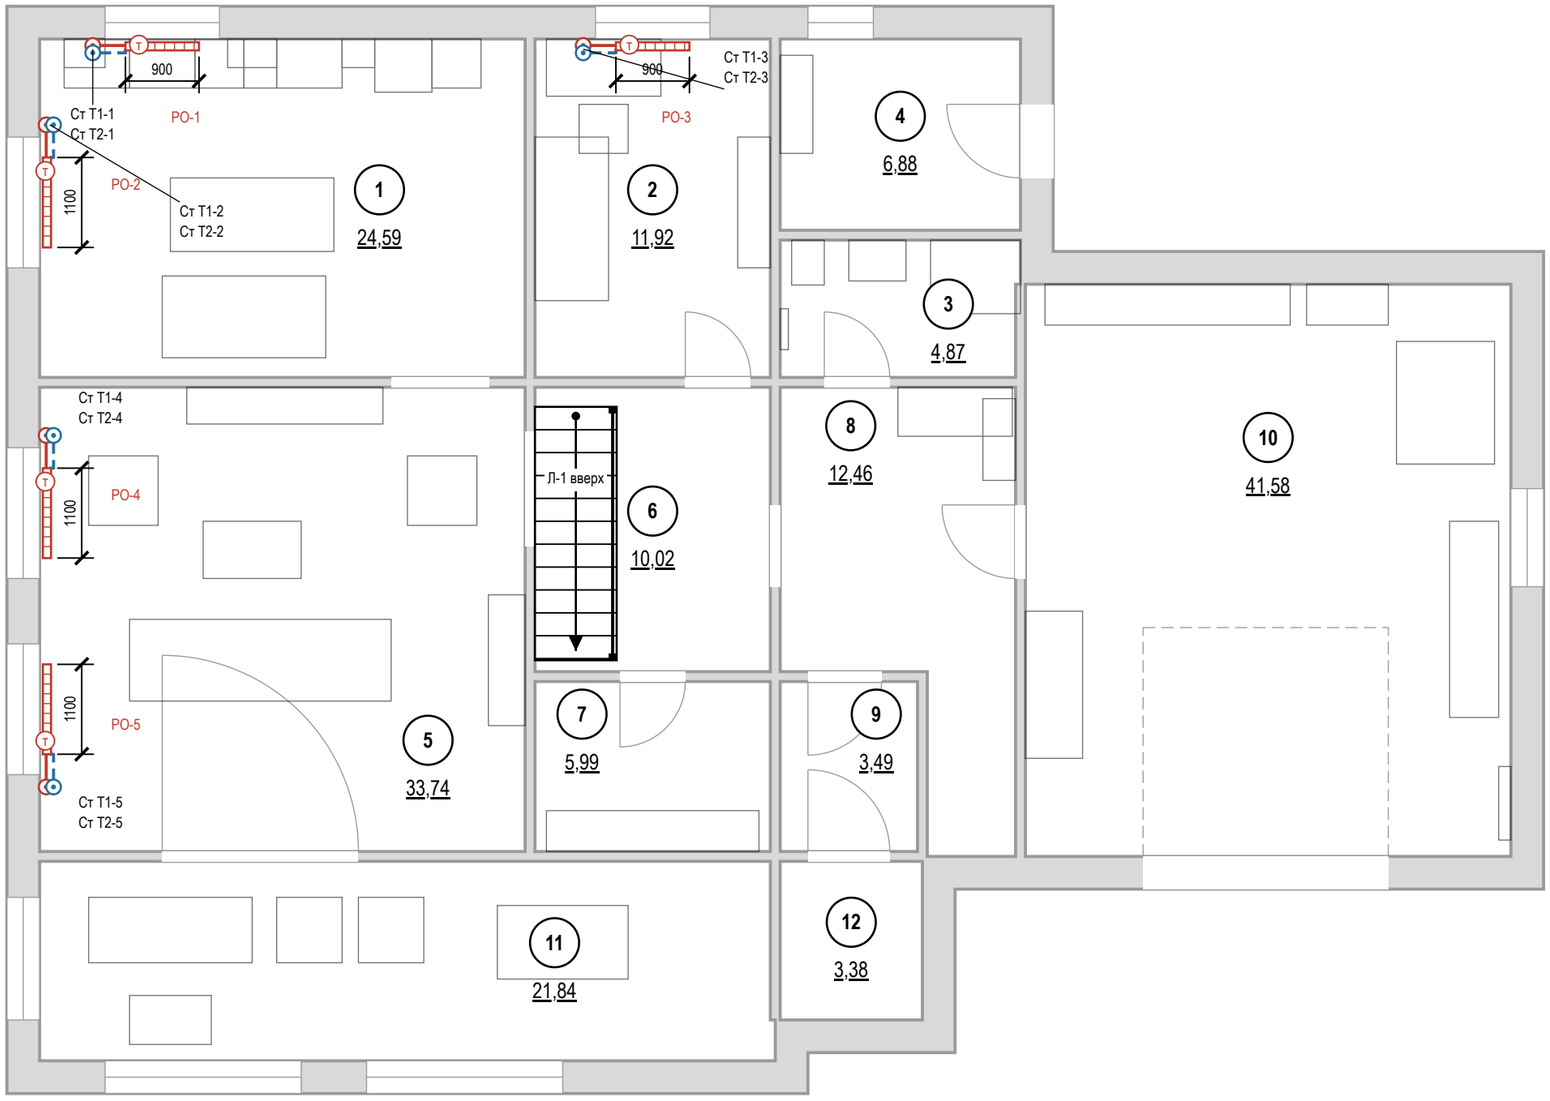


## Условные обозначения

- 1 — номер помещения, площадь м²
- радиатор отопления (марка РО-N, длина по плану)
- клапан с термоголовкой на подаче
- стояк отопления, подающий (Ст Т1-N)
- стояк отопления, обратный (Ст Т2-N)
- Т1 — отопление, подающий трубопровод
- Т2 — отопление, обратный трубопровод

## Ведомость радиаторов

| Марка | Помещение | Тип | Д×В×Г, мм | Низ / стена | Q, Вт |
|---|---|---|---|---|---|
| РО-1 | 1. Кухня-столовая | панельный | 900×600×100 | 120 / 40 | расч. |
| РО-2 | 1. Кухня-столовая | панельный | 1100×600×100 | 120 / 40 | расч. |
| РО-3 | 2. Кабинет-гостевая | панельный | 900×600×100 | 120 / 40 | расч. |
| РО-4 | 5. Гостиная | панельный | 1100×600×100 | 120 / 40 | расч. |
| РО-5 | 5. Гостиная | панельный | 1100×600×100 | 120 / 40 | расч. |

тип и мощность — по теплотехническому расчёту
Низ — от чистого пола, стена — зазор до задней панели, мм.

**Привязки — до обмера**
Стояки отопления в исходных данных не заданы: показаны у откосов окон, подводки принципиально. До черновых работ — обмер стояков и паспорта приборов; лист перевыпустить по факту.

## Примечания

1. Расчёт системы отопления, теплопотерь и подбор приборов — проектная организация с допуском СРО; лист даёт места и привязки.
2. Тип, длина и мощность радиаторов — по теплотехническому расчёту; лист задаёт места, зазоры и подключение.
3. Радиаторы — под каждым окном жилых комнат и кухни, центр по оси проёма, длина 0,7 ширины окна (кратно 100); окончательно — по расчёту.
4. Зазоры радиатора: низ не менее 100 мм от чистого пола, верх не менее 100 мм до подоконника, 30–50 мм от стены до задней панели; центр по оси окна с допуском ±20 мм.
5. Радиаторы не закрывать глухими коробами и мебелью; перенос и замена приборов в многоквартирном доме — переустройство, согласование с управляющей организацией (ЖК РФ ст. 25–26); вынос на лоджию запрещён.
6. Трубы отопления через межквартирные стены не прокладывать (СП 51.13330.2011, п. 9.19); через перекрытия и перегородки — в гильзах.
7. Привязки приборов и подводок — по паспортам приобретённых радиаторов и клапанов, до черновых работ.
8. До закрытия отделкой трубопроводы отопления испытать гидростатическим давлением с оформлением акта (СП 73.13330.2016, 7.2–7.3).

| | | | | | |
|---|---|---|---|---|---|
| | | | | | Проект: Дом 331 м² |
| | Лист | № док. | Подпись | Дата | План отопления · 1-й этаж |
| Дизайнер | Кырлан А.С. | | | 19.10.26 | Стадия: П; Лист: 45; Листов: 156 |

выпуск 18.10.2026 № 8cd922c868 · стр. 45 из 156

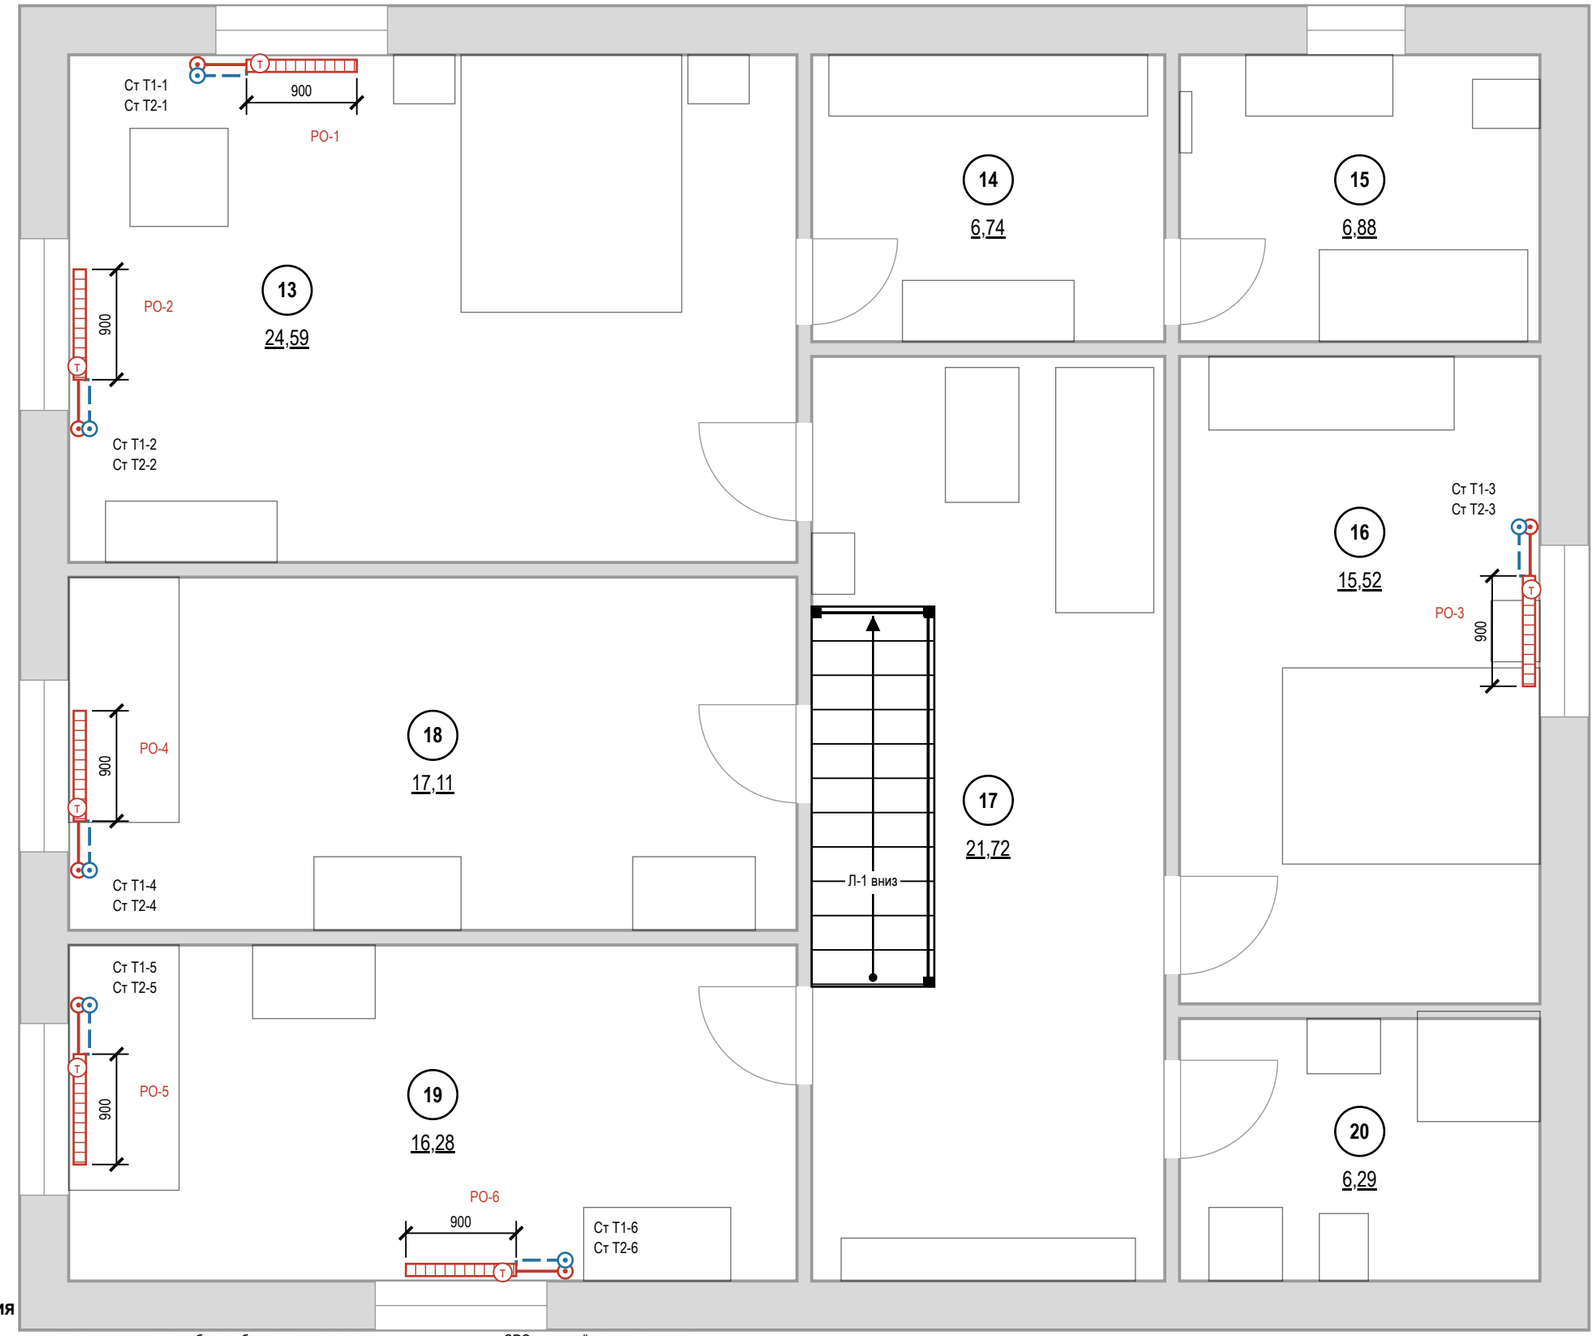


## Условные обозначения

- (1) — номер помещения, площадь м²
- радиатор отопления (марка РО-N, длина по плану)
- (Т) — клапан с термоголовкой на подаче
- стояк отопления, подающий (Ст Т1-N)
- стояк отопления, обратный (Ст Т2-N)
- Т1 — отопление, подающий трубопровод
- Т2 — отопление, обратный трубопровод

## Ведомость радиаторов

| Марка | Помещение | Тип | Д×В×Г, мм | Низ / стена | Q, Вт |
|---|---|---|---|---|---|
| РО-1 | 13. Спальня мастер | панельный | 900×600×100 | 120 / 40 | расч. |
| РО-2 | 13. Спальня мастер | панельный | 900×600×100 | 120 / 40 | расч. |
| РО-3 | 16. Спальня 2 | панельный | 900×600×100 | 120 / 40 | расч. |
| РО-4 | 18. Спальня 3 | панельный | 900×600×100 | 120 / 40 | расч. |
| РО-5 | 19. Спальня 4 | панельный | 900×600×100 | 120 / 40 | расч. |
| РО-6 | 19. Спальня 4 | панельный | 900×600×100 | 120 / 40 | расч. |

тип и мощность — по теплотехническому расчёту
Низ — от чистого пола, стена — зазор до задней панели, мм.

**Привязки — до обмера**
Стояки отопления в исходных данных не заданы: показаны у откосов окон, подводки — принципиально. До черновых работ — обмер стояков и паспорта приборов; лист перевыпустить по факту.

## Примечания

1. Расчёт системы отопления, теплопотерь и подбор приборов — проектная организация с допуском СРО; лист даёт места и привязки.
2. Тип, длина и мощность радиаторов — по теплотехническому расчёту; лист задаёт места, зазоры и подключение.
3. Радиаторы — под каждым окном жилых комнат и кухни, центр по оси проёма, длина 0,7 ширины окна (кратно 100); окончательно — по расчёту.
4. Зазоры радиатора: низ не менее 100 мм от чистого пола, верх не менее 100 мм до подоконника, 30–50 мм от стены до задней панели; центр по оси окна с допуском ±20 мм.
5. Радиаторы не закрывать глухими коробами и мебелью; перенос и замена приборов в многоквартирном доме — переустройство, согласование с управляющей организацией (ЖК РФ ст. 25–26); вынос на лоджию запрещён.
6. Трубы отопления через межквартирные стены не прокладывать (СП 51.13330.2011, п. 9.19); через перекрытия и перегородки — в гильзах.
7. Привязки приборов и подводок — по паспортам приобретённых радиаторов и клапанов, до черновых работ.
8. До закрытия отделкой трубопроводы отопления испытать гидростатическим давлением с оформлением акта (СП 73.13330.2016, 7.2–7.3).

| | | | | | |
|---|---|---|---|---|---|
| | | | | | Проект: Дом 331 м² |
| | Лист | № док. | Подпись | Дата | План отопления · Мансарда |
| Дизайнер | Кырлан А.С. | | | 19.10.26 | Стадия: П; Лист: 46; Листов: 156 |

выпуск 18.10.2026 № 8cd922c868 · стр. 46 из 156

Правка к этому листу

## Отметки по высоте

**±0,000** чистый пол пом. 1, 2, 4–10; отсчёт высот
**−0,015** чистый пол пом. 3, ниже на 15 мм
**−0,030** чистый пол пом. 11, 12, ниже на 30 мм
**плита** верх плиты разный: −0,064, −0,170 (задание на обмер)
**сущ. пол** снимается до плиты; не замерен (задание на обмер)

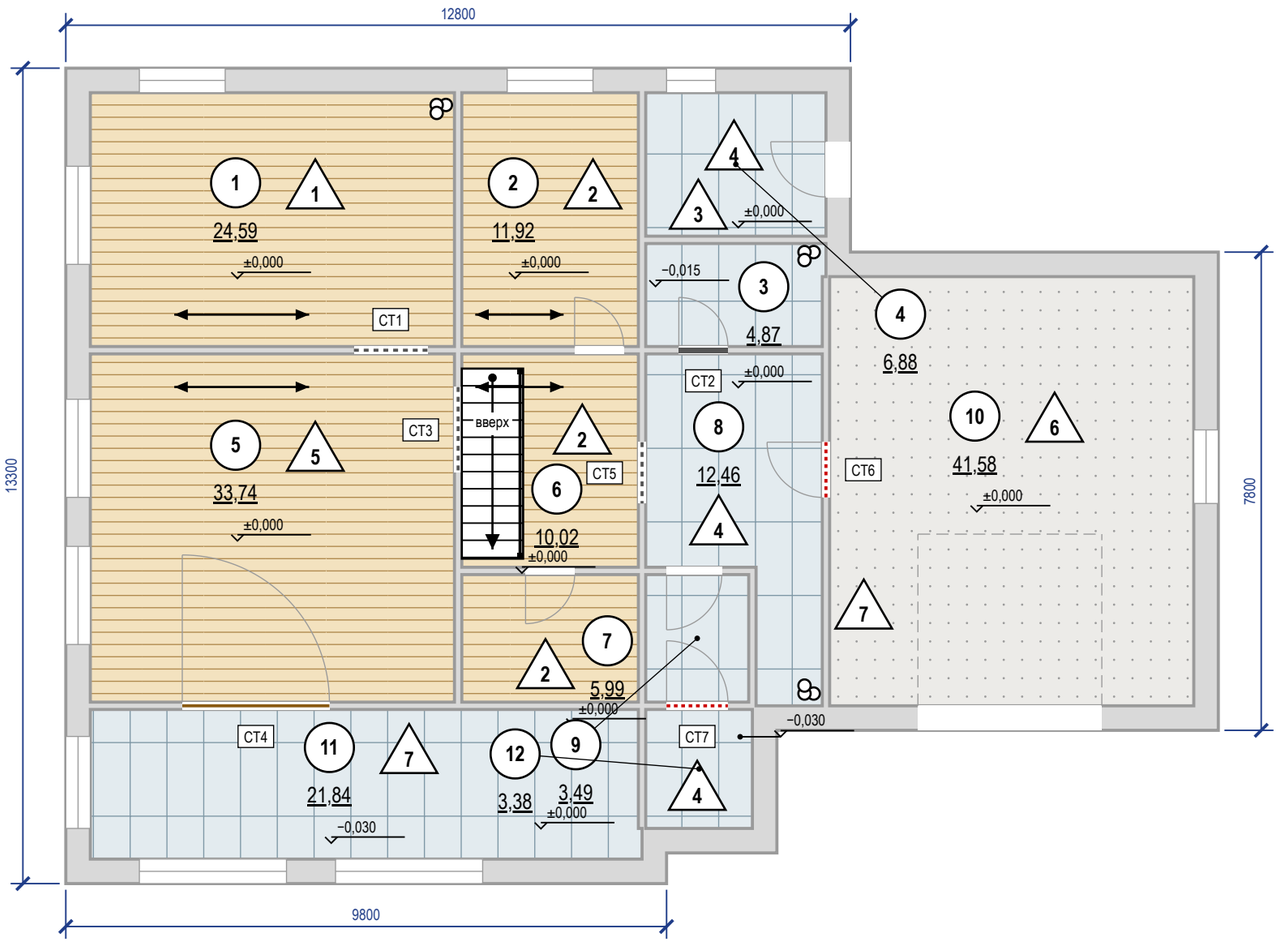


## Экспликация полов

| Номер помещения | Тип пола | Схема пола | Данные элементов пола (наименование, толщина, основание), мм | Площадь, м² |
|---|---|---|---|---|
| 1 | 1 | 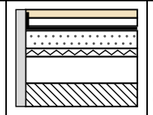 | Инженерная доска дуб на клею — 14<br>Клей паркетный МС-полимерный — 1<br>Гидроизоляция полиуретановая, 2 слоя (зона мойки и острова) — 2<br>Стяжка ЦПС М300 (В22,5), фибра, по звукоизоляции — 53<br>Звукоизоляция — минплита 110 кг/м³ 20<br>Засыпка керамзитовая фр. 0–5, уплотнённая — 80<br>Плита перекрытия монолитная<br>Всего 170 мм; ЧП ±0,000, верх плиты −0,170 | 24,59 |
| 2, 6, 7 | 2 | 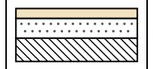 | Инженерная доска на клею — 14<br>Стяжка ЦПС М200 — 50<br>Плита перекрытия<br>Всего 64 мм; ЧП ±0,000, верх плиты −0,064 | 27,93 |
| 3 | 3 | 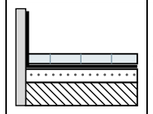 | Керамогранит на клею С2 TE S1 — 14<br>Гидроизоляция обмазочная, 2 слоя, с заведением на стены 200 мм — 2<br>Стяжка ЦПС М200 — 33<br>Плита перекрытия<br>Всего 49 мм; ЧП −0,015, верх плиты −0,064 | 4,87 |
| 4, 8, 9 | 4 | 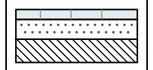 | Керамогранит на клею С2 TE S1 — 14<br>Стяжка ЦПС М200 — 50<br>Плита перекрытия<br>Всего 64 мм; ЧП ±0,000, верх плиты −0,064 | 22,83 |
| 5 | 5 | 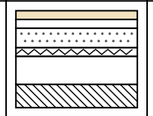 | Инженерная доска дуб на клею — 14<br>Клей паркетный МС-полимерный — 1<br>Стяжка ЦПС М300 (В22,5), фибра, по звукоизоляции — 55<br>Звукоизоляция — минплита 110 кг/м³ 20<br>Засыпка керамзитовая фр. 0–5, уплотнённая — 80<br>Плита перекрытия монолитная<br>Всего 170 мм; ЧП ±0,000, верх плиты −0,170 | 33,74 |
| 10 | 6 | 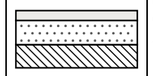 | Наливной полимерный пол с грунтом и кварцевой посыпкой — 3<br>Стяжка ЦПС М300, армированная сеткой — 61<br>Плита перекрытия по грунту<br>Всего 64 мм; ЧП ±0,000, верх плиты −0,064 | 41,58 |
| 11, 12 | 7 | 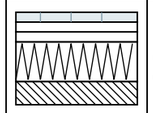 | Керамогранит 600×600×10 — 10<br>Клей плиточный С2 TE S1 (деформируемый) — 5<br>Сборное основание ГВЛВ 2×12,5 — 25<br>Пенополистирол экструзионный 2×50 100<br>Плита перекрытия монолитная<br>Всего 140 мм; ЧП −0,030, верх плиты −0,170 | 25,22 |
| | | | **Итого** | **180,76** |

## Примечания

1. За отметку ±0,000 принят чистый пол, не существующий (блок отметок). Площади — по чистым размерам помещений, м²; размеры — в мм.
2. Стык разнотипных покрытий — по оси дверного полотна (под полотном в закрытом положении); решение стыка — по ведомости стыков.
3. Пол санузлов ниже смежных помещений на 15 мм; гидроизоляция по стяжке с заведением на стены не менее 200 мм (СП 29.13330.2011, п. 7.2), до облицовки — тест проливом и акт скрытых работ.
4. Трубопроводы в конструкции пола не прокладываются: пирог пола 49–170 мм не вмещает выпуски канализации с уклоном — выпуски К1 ведутся по стенам над чистым полом в коробах.
5. Штучные покрытия (инженерная доска): направление — по стрелке; влажность основания по СМ не более 2,0 % (по ТУ изготовителя).
6. Ровность основания — просвет под 2-метровой рейкой не более 2 мм: пом. 1, 2, 5, 6, 7 (инженерная доска), пом. 3, 4, 8, 9 (керамогранит), пом. 10 (наливной пол); 3 мм: пом. 11, 12 (керамогранит); проверить до укладки покрытия (СП 71.13330.2017, табл. 8.5).
7. Плавающая стяжка по звукоизоляции: демпферная (кромочная) лента по контуру помещения, у стояков и колонн — до верха чистого пола (СП 51.13330.2011, п. 9.11); плинтус крепится только к стене.
8. Сетка на плитке — условная, в размер формата; точка старта и раскладка — по листу раскладки плитки.
9. Пироги полов — по экспликации полов: слои сверху вниз, толщины в мм; гидроизоляция мокрых зон — в пироге и в ведомости отделки; схема пола — без масштаба.

| | | | | | |
|---|---|---|---|---|---|
| | | | | | Проект: Дом 331 м² |
| | Лист | № док. | Подпись | Дата | План покрытий пола · 1-й этаж |
| Дизайнер | Кырлан А.С. | | | 19.10.26 | Стадия: П; Лист: 47; Листов: 156 |

выпуск 18.10.2026 № 8cd922c868 · стр. 47 из 156

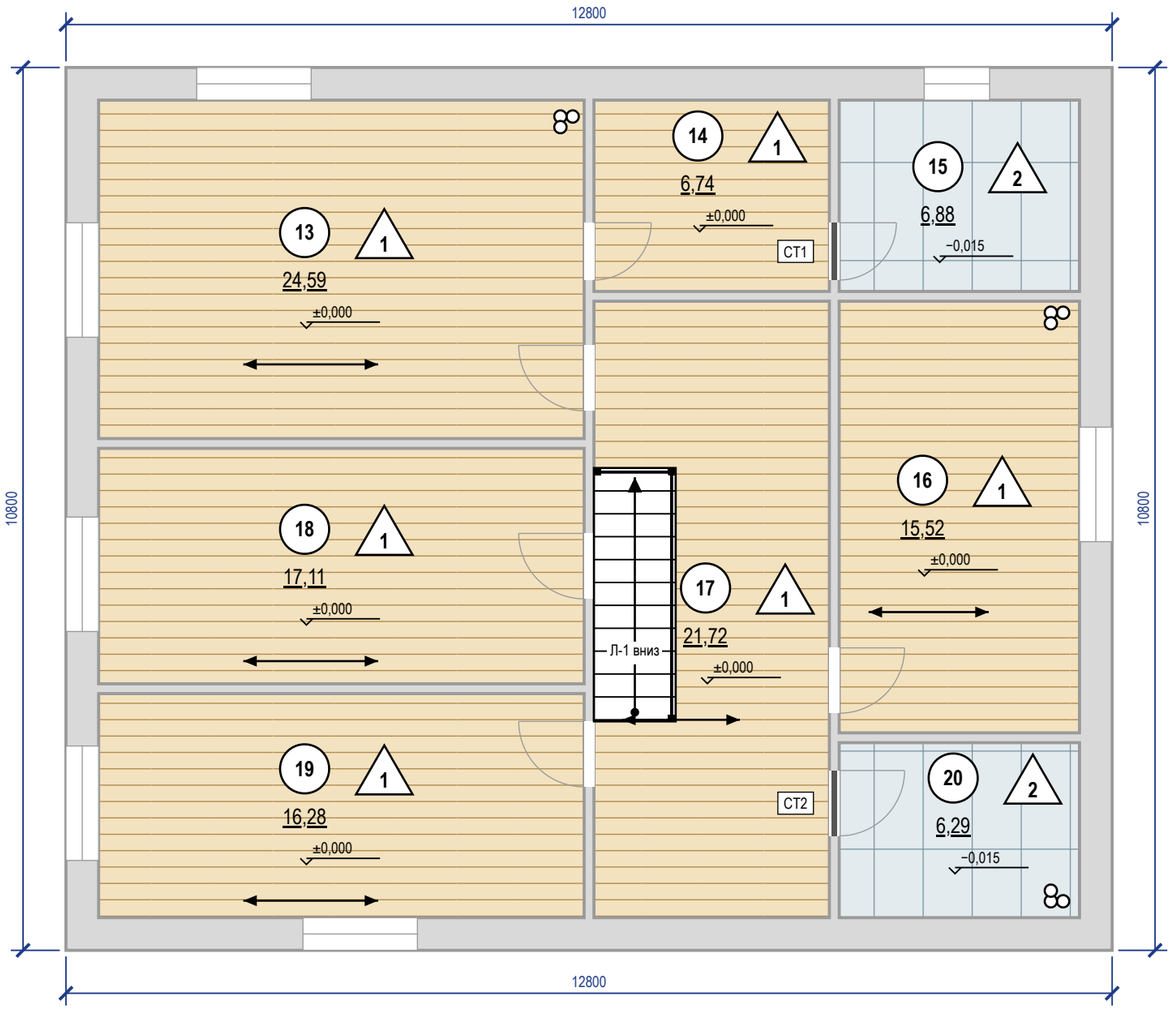


## Экспликация полов

| Номер помещения | Тип пола | Схема пола | Данные элементов пола (наименование, толщина, основание), мм | Площадь, м² |
|---|---|---|---|---|
| 13, 14, 16, 17, 18, 19 | 1 | 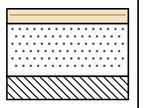 | Инженерная доска на клею — 14<br>Стяжка ЦПС М200 — 50<br>Плита перекрытия<br>Всего 64 мм; ЧП ±0,000, верх плиты −0,064 | 101,96 |
| 15, 20 | 2 | 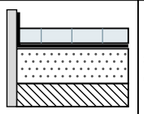 | Керамогранит на клею С2 TE S1 — 14<br>Гидроизоляция обмазочная, 2 слоя, с заведением на стены 200 мм — 2<br>Стяжка ЦПС М200 — 33<br>Плита перекрытия<br>Всего 49 мм; ЧП −0,015, верх плиты −0,064 | 13,17 |
| | | | **Итого** | **115,13** |

## Спецификация плинтусов

| Наименование | Помещения | Длина, м (с запасом) |
|---|---|---|
| Плинтус МДФ под покраску 80×16, крепление к стене, окраска в цвет Farrow & Ball No. 226 | 13, 14, 16, 17 | 67 |
| SX165, h = 69 мм, крепление к стене, окраска в цвет Farrow & Ball No. 226 | 18, 19 | 37 |

## Отметки по высоте

**±0,000** чистый пол пом. 13, 14, 16–19; отсчёт высот
**−0,015** чистый пол пом. 15, 20, ниже на 15 мм
**−0,064** верх плиты — расчёт, не замер (задание на обмер)
**сущ. пол** снимается до плиты; не замерен (задание на обмер)

## Примечания

1. За отметку ±0,000 принят чистый пол, не существующий (блок отметок). Площади — по чистым размерам помещений, м²; размеры — в мм.
2. Стык разнотипных покрытий — по оси дверного полотна (под полотном в закрытом положении); решение стыка — по ведомости стыков.
3. Пол санузлов ниже смежных помещений на 15 мм за счёт меньшей толщины стяжки (верх плиты общий — по экспликации полов); гидроизоляция по стяжке с заведением на стены не менее 200 мм (СП 29.13330.2011, п. 7.2), до облицовки — тест проливом и акт скрытых работ.
4. Трубопроводы в конструкции пола не прокладываются: пирог пола 49–64 мм не вмещает выпуски канализации с уклоном — выпуски К1 ведутся по стенам над чистым полом в коробах.
5. Штучные покрытия (инженерная доска): направление — по стрелке; влажность основания по СМ не более 2,0 % (по ТУ изготовителя).
6. Ровность основания — просвет под 2-метровой рейкой не более 2 мм: пом. 13, 14, 16, 17, 18, 19 (инженерная доска), пом. 15, 20 (керамогранит); проверить до укладки покрытия (СП 71.13330.2017, табл. 8.5).
7. Сетка на плитке — условная, в размер формата; точка старта и раскладка — по листу раскладки плитки.
8. Пироги полов — по экспликации полов: слои сверху вниз, толщины в мм; гидроизоляция мокрых зон — в пироге и в ведомости отделки; схема пола — без масштаба.

| | | | | | |
|---|---|---|---|---|---|
| | | | | | Проект: Дом 331 м² |
| | Лист | № док. | Подпись | Дата | |
| Дизайнер | Кырлан А.С. | | | 19.10.26 | План покрытий пола · Мансарда |
| | | | | | Стадия: П; Лист: 48; Листов: 156 |

выпуск 18.10.2026 № 8cd922c868 · стр. 48 из 156

Правка к этому листу

Фрагмент 1. Санузел 1 этажа (пом. 3). Пол 600×600, шов 2 мм, М 1:40

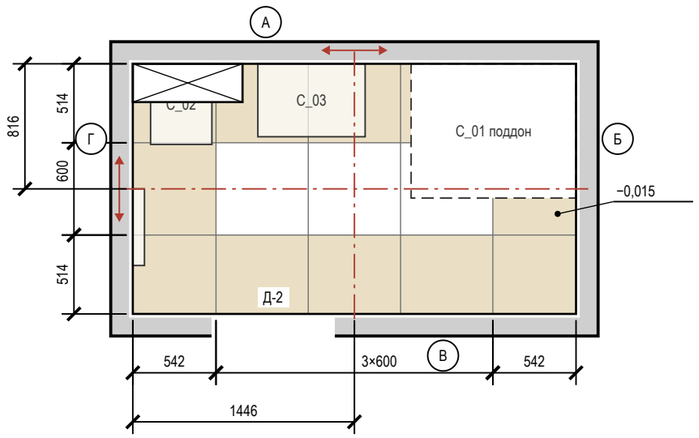


Фрагмент 2. Санузел мастер (пом. 15). Пол 600×600, шов 2 мм, М 1:40

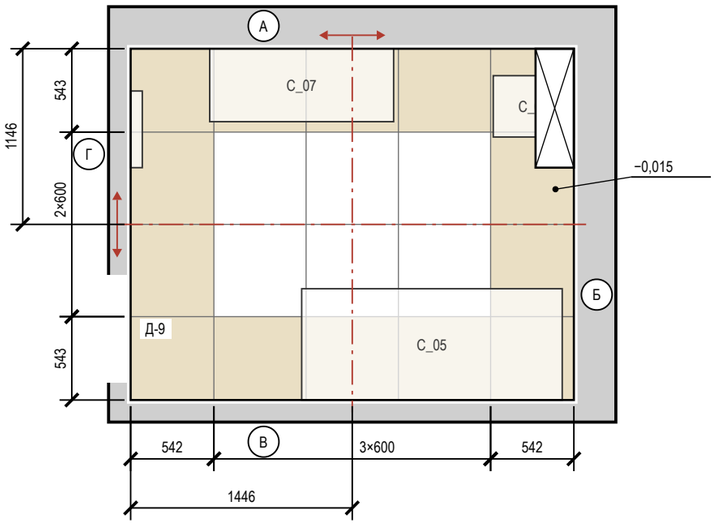


Фрагмент 3. Санузел 2 (пом. 20). Пол 600×600, шов 2 мм, М 1:40

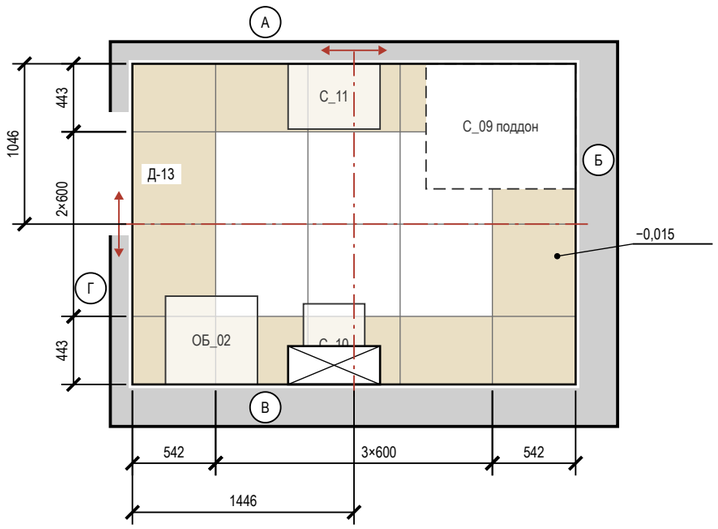


## Ведомость плитки

| Помещение, поверхность | Плитка, код | Формат | Шов | S, м² | Целых | Подр. | С запасом |
|---|---|---|---|---|---|---|---|
| Санузел 1 этажа, пол | аналог: керамогранит под травертин | 600×600 | 2 | 4,87 | 2 | 12 | 16 |
| Санузел 1 этажа, стены А–Г | аналог: керамогранит под травертин | 600×1200 | 2 | 19,67 | 11 | 19 | 34 |
| Санузел 1 этажа, короб инсталляции | аналог: керамогранит под травертин | 600×1200 | 2 | 1,64 | 0 | 6 | 7 |
| Санузел мастер, пол | аналог: керамогранит под травертин | 600×600 | 2 | 6,88 | 6 | 14 | 22 |
| Санузел мастер, стены А–Г | аналог: керамогранит под травертин | 600×1200 | 2 | 19,01 | 14 | 21 | 39 |
| Санузел мастер, короб инсталляции | аналог: керамогранит под травертин | 600×1200 | 2 | 1,73 | 0 | 6 | 7 |
| Санузел 2, пол | аналог: керамогранит под травертин | 600×600 | 2 | 6,29 | 5 | 14 | 21 |
| Санузел 2, стены А–Г | аналог: керамогранит под травертин | 600×1200 | 2 | 17,04 | 14 | 21 | 39 |
| Санузел 2, короб инсталляции | аналог: керамогранит под травертин | 600×1200 | 2 | 1,47 | 1 | 3 | 5 |
| Котельная, пол | A8UZ | 600×1200 | 2 | 6,88 | 0 | 10 | 11 |
| Прихожая, пол | A8UZ | 600×1200 | 2 | 12,46 | 3 | 12 | 17 |
| Тамбур, пол | A8UZ | 600×1200 | 2 | 3,49 | 0 | 6 | 7 |
| Веранда, пол | A8UZ | 600×1200 | 2 | 21,84 | 13 | 32 | 50 |
| Крыльцо, пол | A8UZ | 600×1200 | 2 | 3,38 | 0 | 6 | 7 |
| Итого 600×600 | | | | 18,04 | 13 | 40 | 59 |
| **Итого 600×1200** | | | | **108,60** | **56** | **142** | **223** |

## Ведомость материалов

| Материал | Класс, код | Норма расхода | Кол-во |
|---|---|---|---|
| Затирка | CG2WA Mapei Ultracolor Plus 132 | (a+b)/ab·шов·t·1,6 | 6,9 кг |
| Затирка | CG2WA | (a+b)/ab·шов·t·1,6 | 3,8 кг |
| Клей | C2 TE S1 Ceresit CM 17 | 1,5 кг/м²·мм, слой 5 | 682 кг (28 меш.) |
| Клей | C2 TE S1 | 1,5 кг/м²·мм, слой 5 | 370 кг (15 меш.) |
| Гидроизоляция | обмазочная, 2 слоя: пол, стены по периметру и зоны замачивания | по ТУ | 43,1 м² |
| Демпф. лента | по периметру пола из плитки | | 85,5 м |

## Условные обозначения

- плитка целая; тонкая линия — шов
- плитка с подрезкой (размер — на цепочке)
- ось старта; стрелки — направление укладки
- сантехприбор: габарит, высота по практике
- поддон душа — плитку пола под ним не кладут
- короб инсталляции: плитка пола — до короба
- отметка чистого пола на полке выноски, м
- (А) обозначение стены А–Г (как на развёртках)

## Примечания

1. Раскладка от чистовых размеров: стены санузлов теряют 10 + 5 + 9 = 24 мм на сторону (штукатурка, клей, плитка); подрезки — чистые, без шва.
2. Старт — от центра помещения (штрихпунктир, стрелки — направление укладки); размер старта — от чистовых стен Г и А.
3. Раскладка пола «Котельная» и пола «Прихожая» и пола «Тамбур» и пола «Веранда» и пола «Крыльцо» — на листе «Раскладка плитки. Котельная. Прихожая. Тамбур. Веранда. Крыльцо».
4. Калибр партии не задан — до укладки замерить (рабочий размер W, ГОСТ 13996-2019) и пересчитать подрезки.
5. Количество: целые по раскладке + по одной на подрезку, запас 10 %; один артикул — одна партия и тон. Исключены поддон, короб, проёмы и места за коробом; S — по чистым граням: стены нетто = зона облицовки по ведомости отделки − место за коробом инсталляции 2,51 м² (плитку за коробом не кладут), короб — отдельной строкой.
6. Клей C2 TE S1 Ceresit CM 17; C2 TE S1 (ГОСТ Р 56387-2018), затирка CG2WA Mapei Ultracolor Plus 132; CG2WA; расход — по ТУ выбранной марки.
7. Гидроизоляция: пол и стены 200 мм от ЧП; у душа — до 2000 и 500 мм за поддон, над ванной — до 2000 и 300 мм за борт (см. развёртки); акт скрытых работ, пролив 24 ч.
8. Швы пола совмещены со швами стены А; по периметру — демпферная лента.
9. Отметка чистого пола −0,015, порог 15 мм; стык с соседним покрытием — по оси полотна двери.

| | | | | | |
|---|---|---|---|---|---|
| | | | | | Проект: Дом 331 м² |
| | Лист | № док. | Подпись | Дата | |
| Дизайнер | Кырлан А.С. | | | 19.10.26 | Раскладка плитки. Планы полов |

| Стадия | Лист | Листов |
|---|---|---|
| П | 49 | 156 |

Правка к этому листу

**Фрагмент 1. Котельная (пом. 4). Пол 600×1200, шов 2 мм, М 1:50**

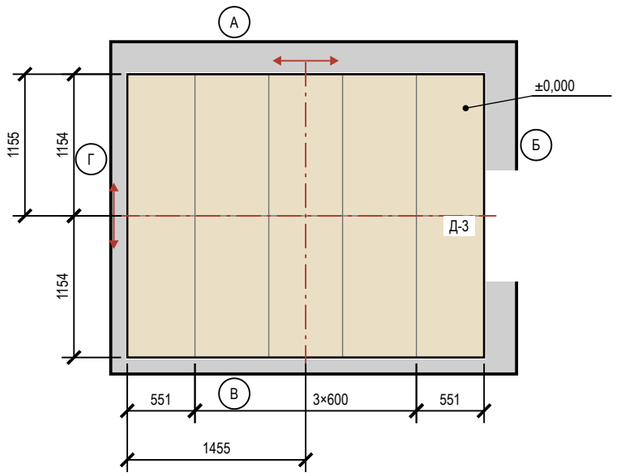


**Фрагмент 2. Прихожая (пом. 8). Пол 600×1200, шов 2 мм, М 1:50**

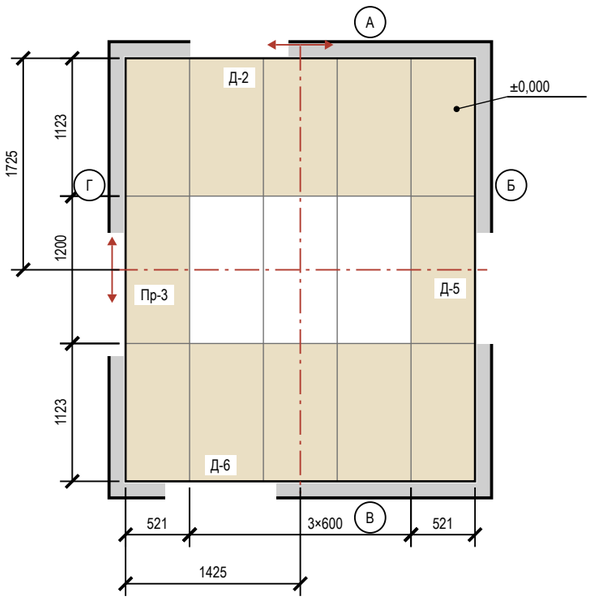


**Фрагмент 3. Тамбур (пом. 9). Пол 600×1200, шов 2 мм, М 1:50**

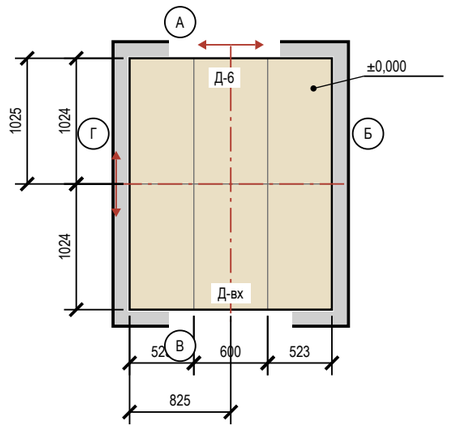


## Условные обозначения

- плитка целая; тонкая линия — шов
- плитка с подрезкой (размер — на цепочке)
- ось старта; стрелки — направление укладки
- отметка чистого пола на полке выноски, м
- А — обозначение стены А–Г (как на развёртках)

**Фрагмент 4. Веранда (пом. 11). Пол 600×1200, шов 2 мм, М 1:50**

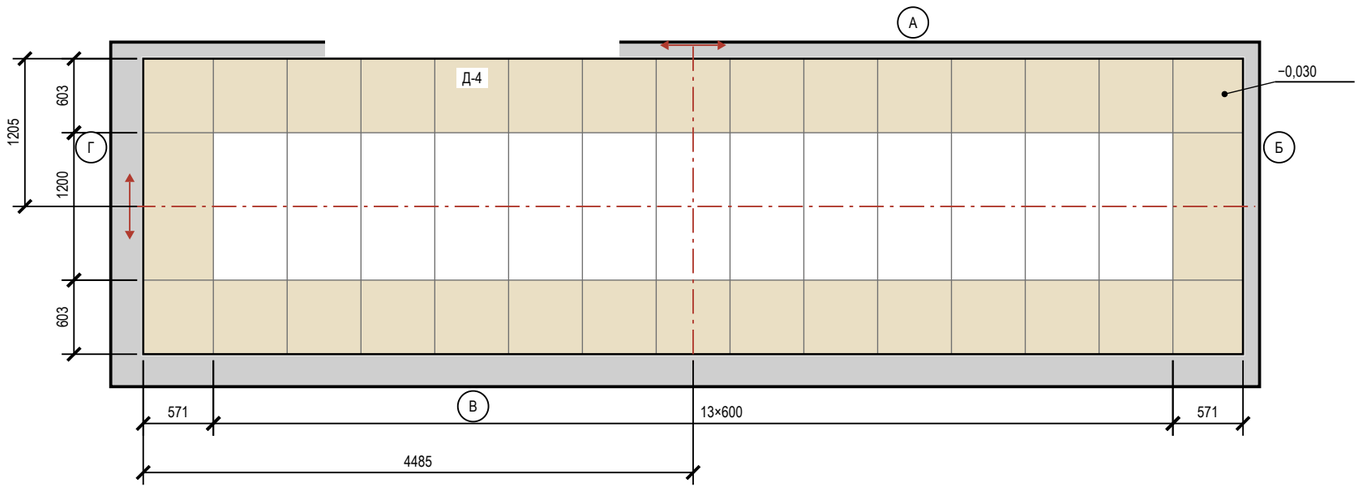


## Подсчёт плитки

| Поверхность | Формат | S, м² | Целых | Подр. | С запасом |
|---|---|---|---|---|---|
| Котельная, пол | 600×1200 | 6,88 | 0 | 10 | 11 |
| Прихожая, пол | 600×1200 | 12,46 | 3 | 12 | 17 |
| Тамбур, пол | 600×1200 | 3,49 | 0 | 6 | 7 |
| Веранда, пол | 600×1200 | 21,84 | 13 | 32 | 50 |

## Примечания

1. Котельная: керамогранит 600×1200, длинная сторона — вдоль стен Б и Г, шов 2 мм, прямая раскладка от центра. Стены окрашены: раскладка от чистового контура минус штукатурка и шпаклёвка 15 мм на сторону (принято); подрезки 551 / 1154 мм, срез — под плинтус.
2. Котельная: деформационный зазор по периметру 8–10 мм под плинтусом; в проёмах — стык с соседним покрытием по оси полотна двери. Клей C2 TE S1, затирка CG2WA.
3. Прихожая: керамогранит 600×1200, длинная сторона — вдоль стен Б и Г, шов 2 мм, прямая раскладка от центра. Стены окрашены: раскладка от чистового контура минус штукатурка и шпаклёвка 15 мм на сторону (принято); подрезки 521 / 1123 мм, срез — под плинтус.
4. Прихожая: деформационный зазор по периметру 8–10 мм под плинтусом; в проёмах — стык с соседним покрытием по оси полотна двери. Клей C2 TE S1, затирка CG2WA.
5. Тамбур: керамогранит 600×1200, длинная сторона — вдоль стен Б и Г, шов 2 мм, прямая раскладка от центра. Стены окрашены: раскладка от чистового контура минус штукатурка и шпаклёвка 15 мм на сторону (принято); подрезки 523 / 1024 мм, срез — под плинтус.
6. Тамбур: деформационный зазор по периметру 8–10 мм под плинтусом; в проёмах — стык с соседним покрытием по оси полотна двери. Клей C2 TE S1, затирка CG2WA.
7. Веранда: керамогранит 600×1200, длинная сторона — вдоль стен Б и Г, шов 2 мм, прямая раскладка от центра. Стены окрашены: раскладка от чистового контура минус штукатурка и шпаклёвка 15 мм на сторону (принято); подрезки 571 / 603 мм, срез — под плинтус.
8. Веранда: деформационный зазор по периметру 8–10 мм под плинтусом; в проёмах — стык с соседним покрытием по оси полотна двери. Клей C2 TE S1, затирка CG2WA.
9. Клей, затирка и итог по форматам — в ведомостях листа «Раскладка плитки. Планы полов».

| | Лист | № док. | Подпись | Дата |
|---|---|---|---|---|
| Дизайнер | Кырлан А.С. | | | 19.10.26 |

Проект: Дом 331 м²

Раскладка плитки. Котельная. Прихожая. Тамбур. Веранда

| Стадия | Лист | Листов |
|---|---|---|
| П | 50 | 156 |

выпуск 18.10.2026 № 8cd922c868 · стр. 50 из 156

Правка к этому листу

| | | | | | | |
|---|---|---|---|---|---|---|
| | | | | | Проект: Дом 331 м² | |
| | Лист | № док. | Подпись | Дата | Визуализация. Вид сверху | Стадия / Лист / Листов |
| Дизайнер | Кырлан А.С. | | | 19.10.26 | | П / 51 / 156 |

выпуск 18.10.2026 № 8cd922c868 · стр. 51 из 156

Правка к этому листу

| | | | | | |
|---|---|---|---|---|---|
| | | | | | Проект: Дом 331 м² |
| | Лист | № док. | Подпись | Дата | |
| Дизайнер | Кырлан А.С. | | | 19.10.26 | Визуализация. Вид сверху |

| Стадия | Лист | Листов |
|---|---|---|
| П | 52 | 156 |

выпуск 18.10.2026 № 8cd922c868 · стр. 52 из 156

Правка к этому листу

| | | | | | |
|---|---|---|---|---|---|
| | | | | | Проект: Дом 331 м² |
| | Лист | № док. | Подпись | Дата | Визуализация: Кухня-столовая |
| Дизайнер | Кырлан А.С. | | | 19.10.26 | |

| Стадия | Лист | Листов |
|---|---|---|
| П | 53 | 156 |

выпуск 18.10.2026 № 8cd922c868 · стр. 53 из 156

Правка к этому листу

| | | | | | | |
|---|---|---|---|---|---|---|
| | | | | | Проект: Дом 331 м² | |
| | Лист | № док. | Подпись | Дата | | |
| Дизайнер | Кырлан А.С. | | | 19.10.26 | Визуализация: Кухня-столовая | Стадия / Лист / Листов |
| | | | | | | П / 54 / 156 |

выпуск 18.10.2026 № 8cd922c868 · стр. 54 из 156

Правка к этому листу

## Развёртка стены А

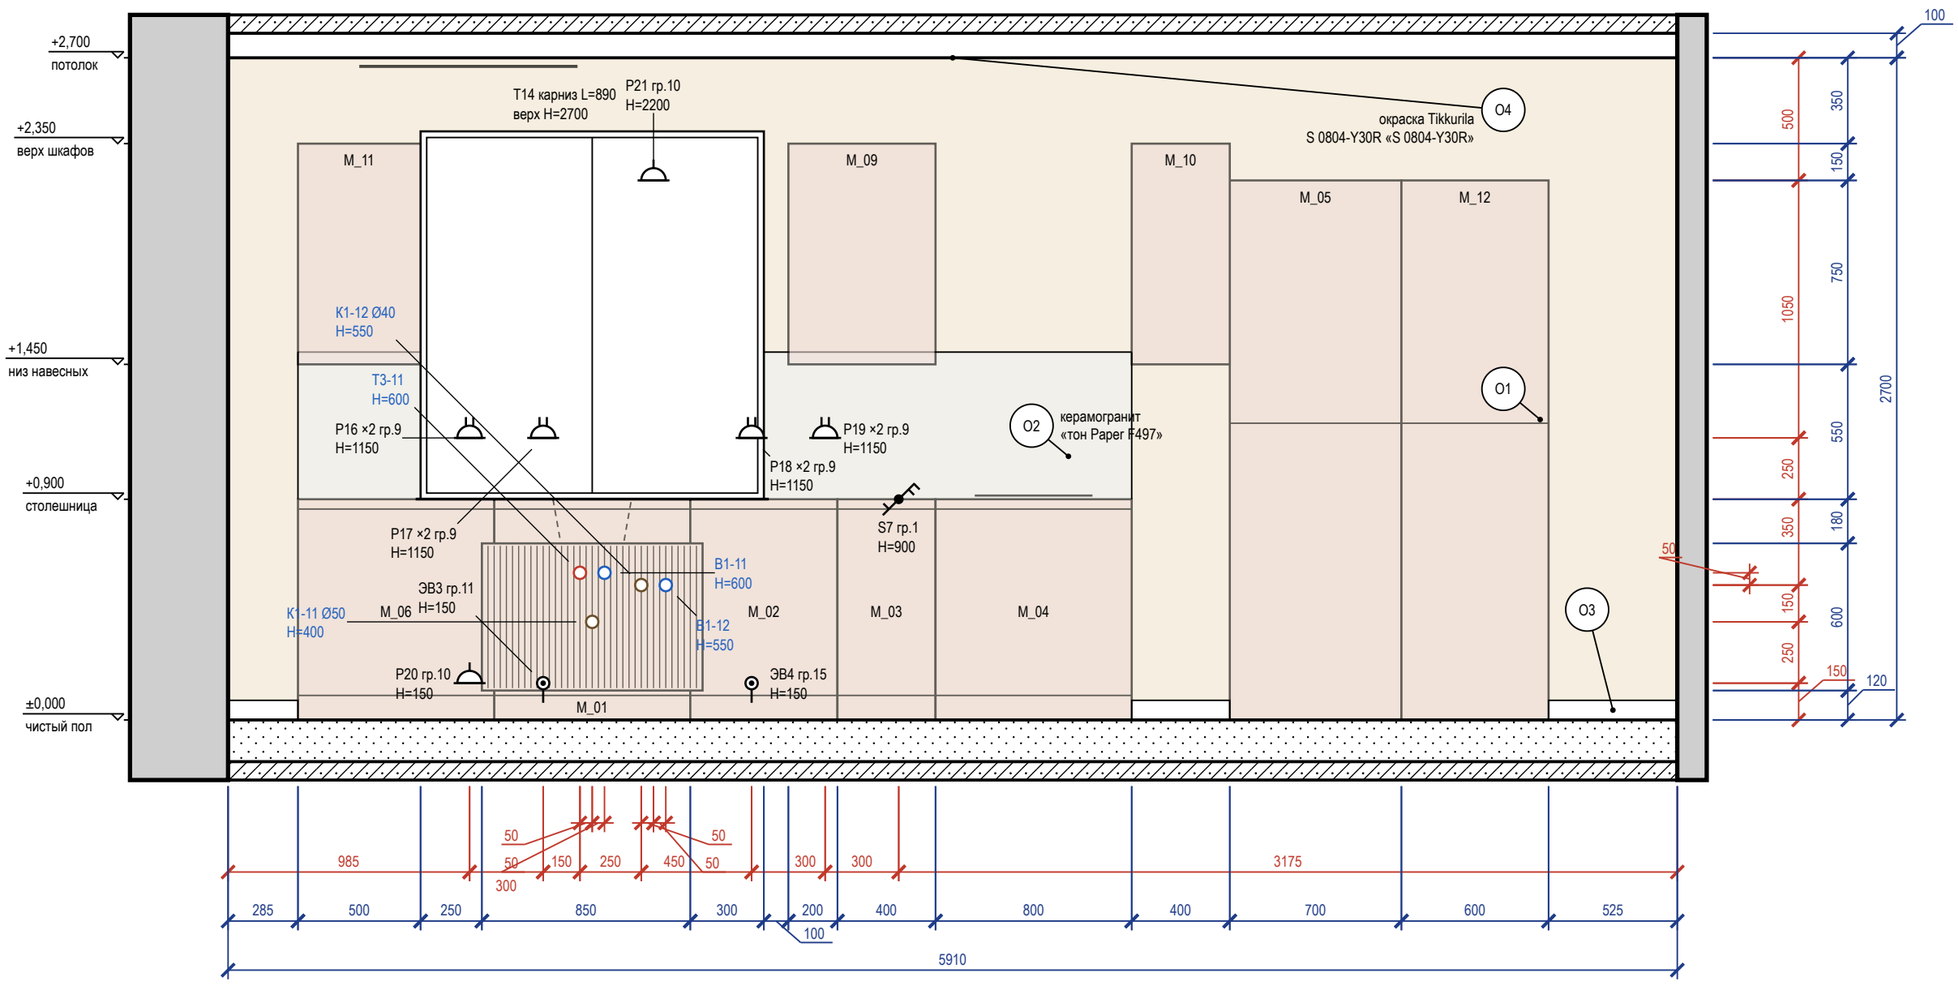


### Схема развёрток (М 1:100)

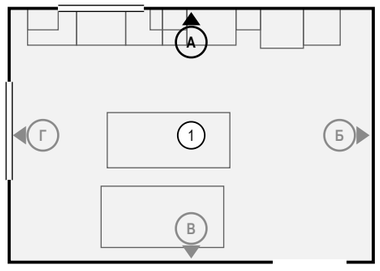


### Ведомость отделки (на листе)

| Марка | Поверхность | Материал, изделие | Цвет, код | Кол. |
|---|---|---|---|---|
| O1 | стены | окраска, Tikkurila Luja 7, шелковисто-матовая, подготовка K3 | NCS S 0804-Y30R «S 0804-Y30R» | 11,8 м² |
| O2 | фартук | керамогранит, аналог: керамогранит матовый, тон F497, затирка CG2WA | #F1F1EC «тон Paper F497» | 1,2 м² |
| O3 | плинтус | плинтус МДФ, h 80 мм, аналог: плинтус МДФ под окраску 80×16 мм, полуглянцевая | NCS S 0804-Y30R «S 0804-Y30R» | 1,2 м |
| O4 | потолок | окраска, Tikkurila Luja 7, матовая, подготовка Q3 | NCS S 0804-Y30R «S 0804-Y30R» | 24,6 м² |

Визуализация этой стены — лист 53

### Примечания

1. Размеры — в мм от чистовых поверхностей стен; условные обозначения и общие указания — лист 2.
2. Выводы ВК — коды и высоты по листу выводов сантехники.
3. Карнизы (шины) — по ведомости текстиля декоратора; длина L и верх H — по развёртке, крепление — до окраски потолка.
4. Выводы кухонной техники — по утверждённому проекту кухни: привязки выводов даются от осей модулей гарнитура.

| | | | | | |
|---|---|---|---|---|---|
| | | | | | Проект: Дом 331 м² |
| | Лист | № док. | Подпись | Дата | Развёртка стены А. Кухня-столовая (пом. 1), кухонный фронт |
| Дизайнер | Кырлан А.С. | | | 19.10.26 | |

| Стадия | Лист | Листов |
|---|---|---|
| П | 55 | 156 |

выпуск 18.10.2026 № 8cd922c868 · стр. 55 из 156

Правка к этому листу

## Развёртка стены Б

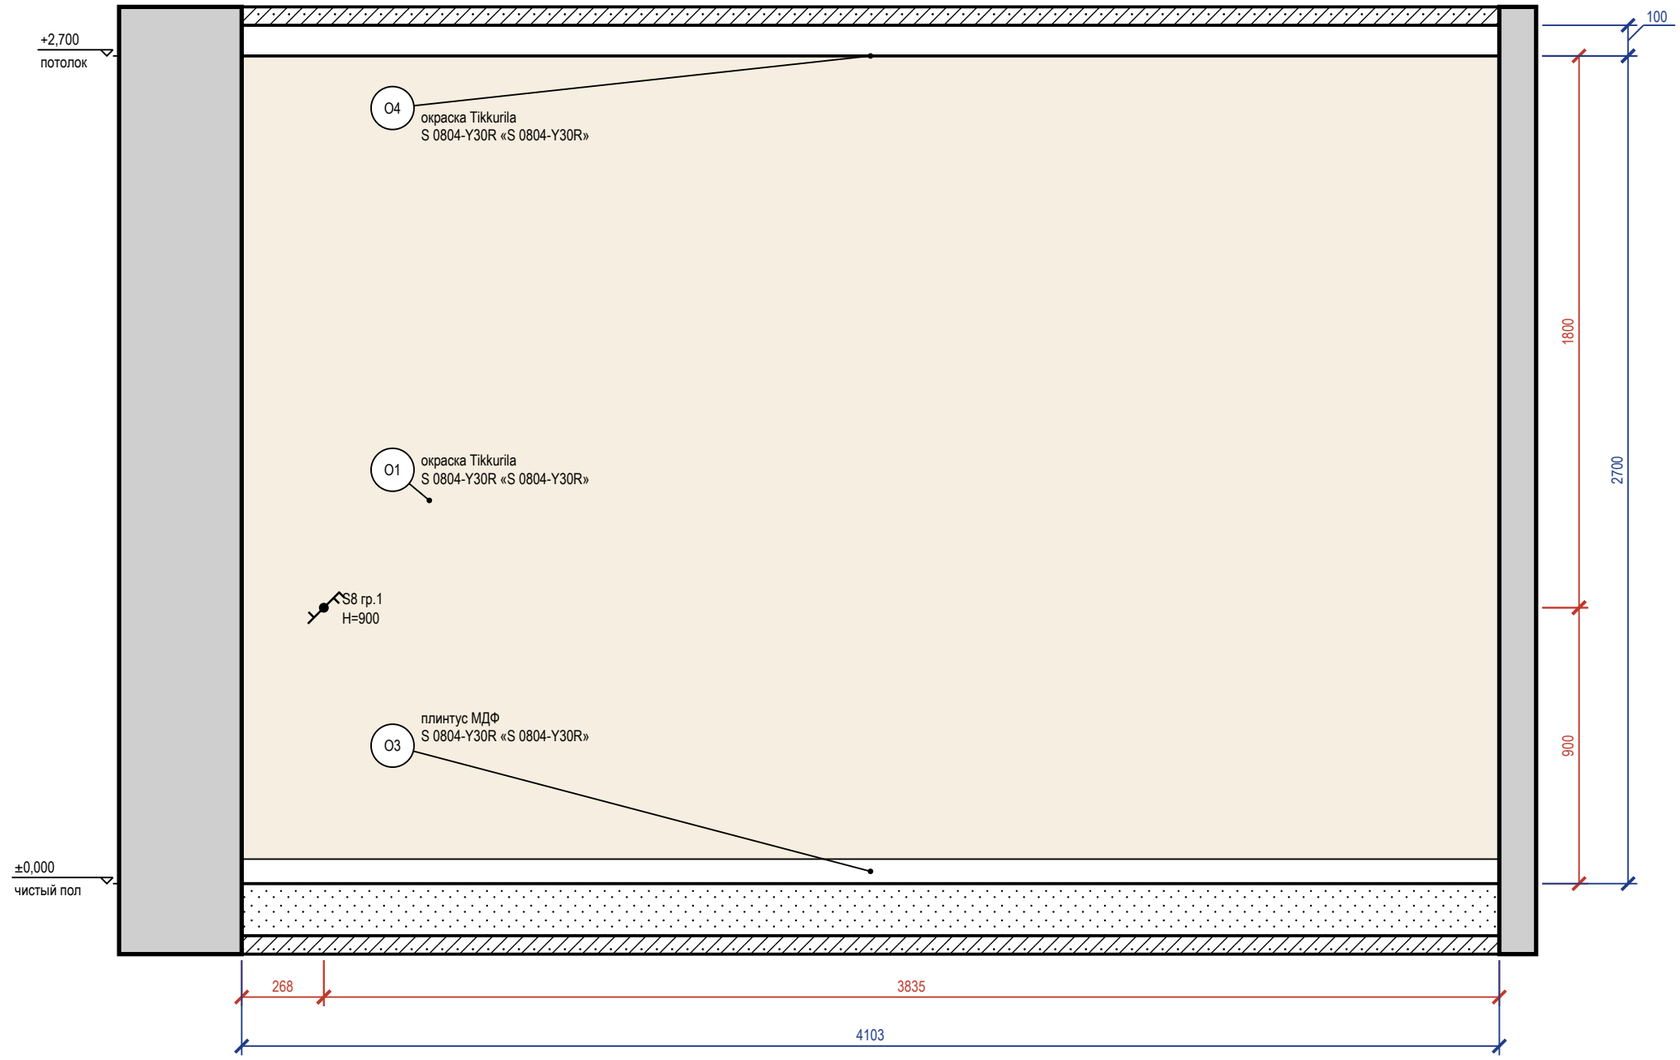


## Схема развёрток (М 1:100)

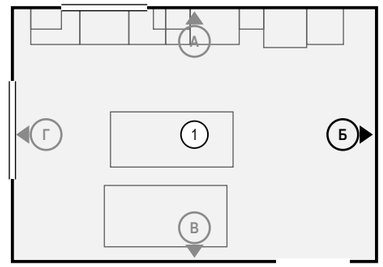


## Ведомость отделки (на листе)

| Марка | Поверхность | Материал, изделие | Цвет, код | Кол. |
|---|---|---|---|---|
| О1 | стены | окраска, Tikkurila Luja 7, шелковисто-матовая, подготовка К3 | NCS S 0804-Y30R «S 0804-Y30R» | 11,1 м² |
| О3 | плинтус | плинтус МДФ, h 80 мм, аналог: плинтус МДФ под окраску 80×16 мм, полуглянцевая | NCS S 0804-Y30R «S 0804-Y30R» | 4,1 м |
| О4 | потолок | окраска, Tikkurila Luja 7, матовая, подготовка Q3 | NCS S 0804-Y30R «S 0804-Y30R» | 24,6 м² |

## Примечания

1. Размеры — в мм от чистовых поверхностей стен; условные обозначения и общие указания — лист 2.

| | | | | | |
|---|---|---|---|---|---|
| | | | | | Проект: Дом 331 м² |
| | Лист | № док. | Подпись | Дата | Развёртка стены Б. Кухня-столовая (пом. 1) |
| Дизайнер | Кырлан А.С. | | | 19.10.26 | |

| Стадия | Лист | Листов |
|---|---|---|
| П | 56 | 156 |

выпуск 18.10.2026 № 8cd922c868 · стр. 56 из 156

Правка к этому листу

## Развёртка стены В

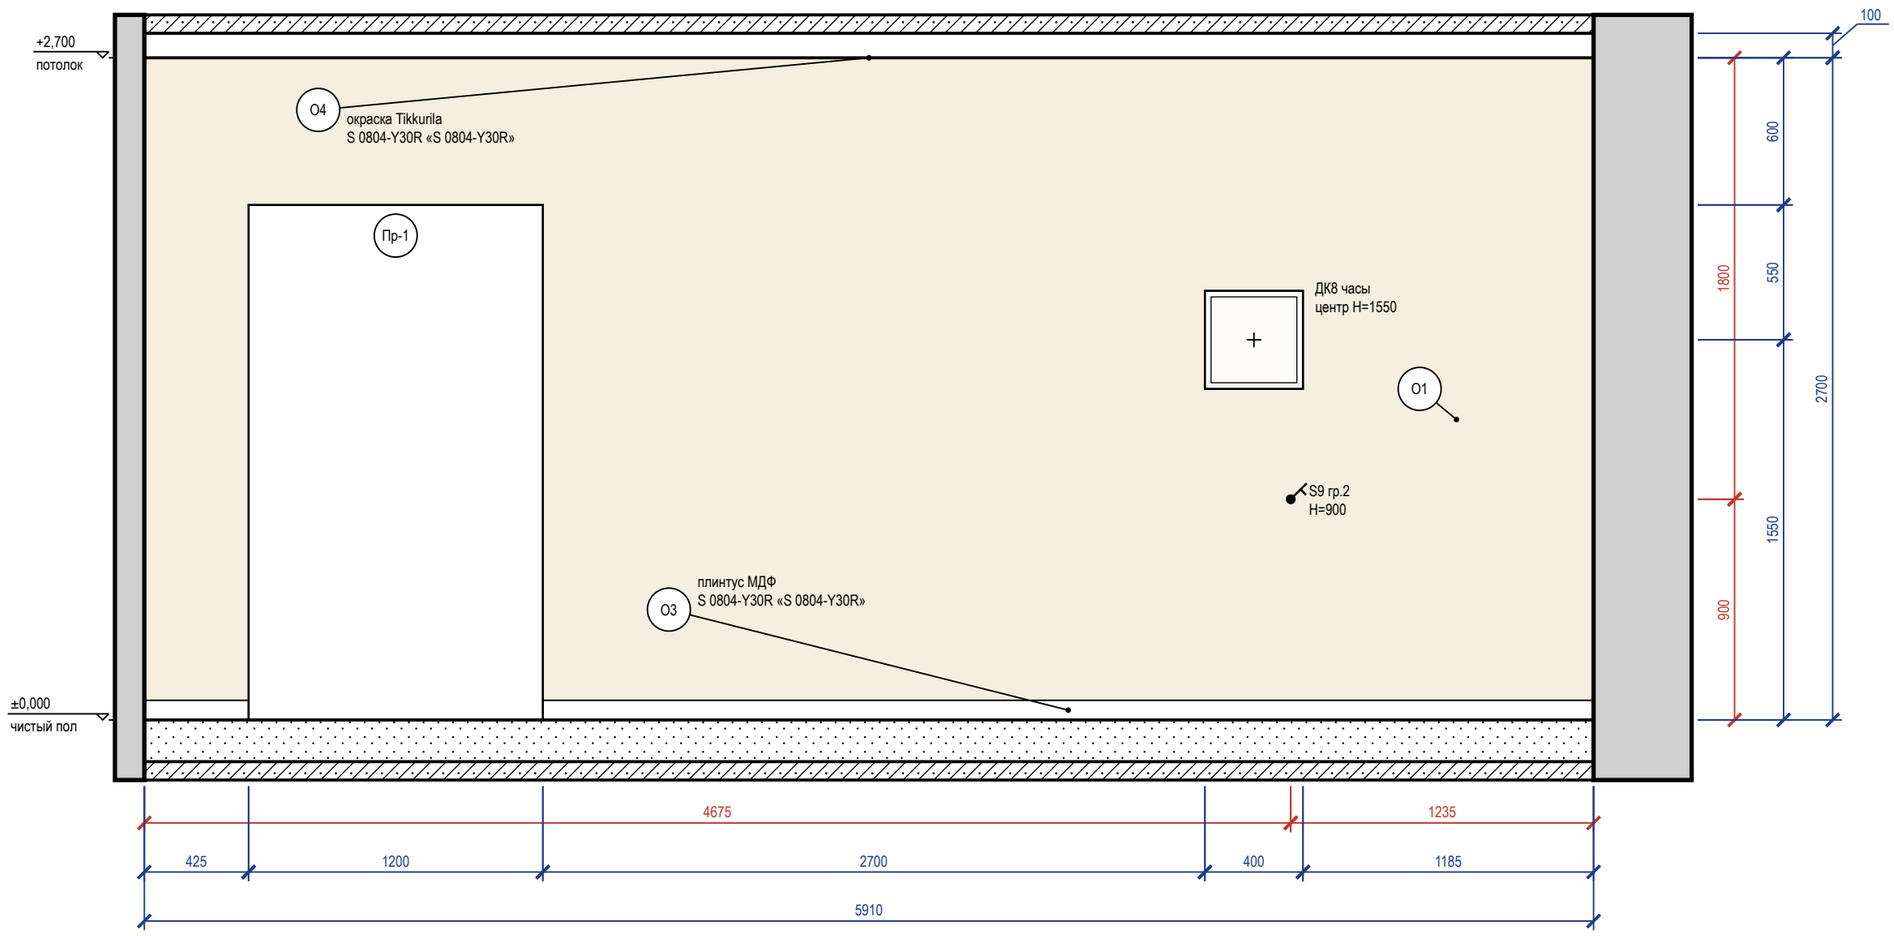


### Схема развёрток (М 1:100)

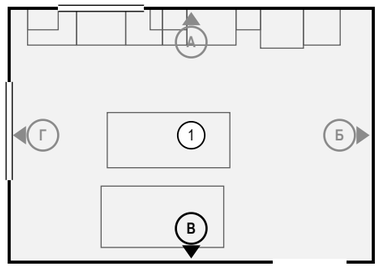


### Ведомость отделки (на листе)

| Марка | Поверхность | Материал, изделие | Цвет, код | Кол. |
|---|---|---|---|---|
| О1 | стены | окраска, Tikkurila Luja 7, шелковисто-матовая, подготовка К3 | NCS S 0804-Y30R «S 0804-Y30R» | 13,4 м² |
| О3 | плинтус | плинтус МДФ, h 80 мм, аналог: плинтус МДФ под окраску 80×16 мм, полуглянцевая | NCS S 0804-Y30R «S 0804-Y30R» | 4,7 м |
| О4 | потолок | окраска, Tikkurila Luja 7, матовая, подготовка Q3 | NCS S 0804-Y30R «S 0804-Y30R» | 24,6 м² |

Визуализация этой стены

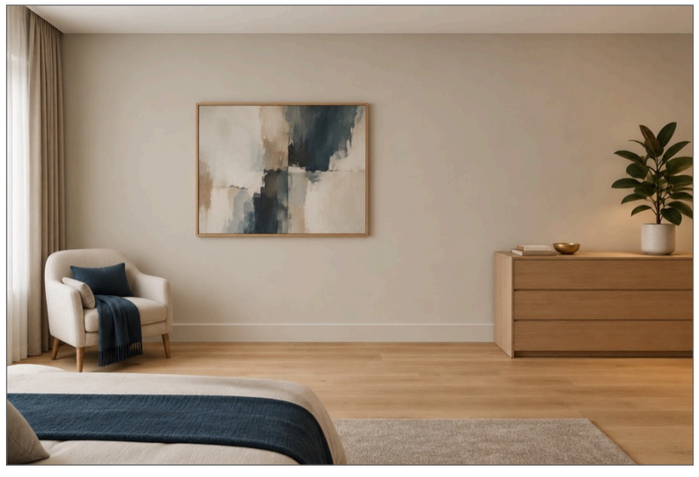

### Примечания

1. Размеры — в мм от чистовых поверхностей стен; условные обозначения и общие указания — лист 2.
2. Картины и зеркала крепить к основанию по паспорту изделия (закладные и анкеры — в перечне скрытых работ); крест — ось центра предмета.

| | | | | | |
|---|---|---|---|---|---|
| | | | | | Проект: Дом 331 м² |
| | Лист | № док. | Подпись | Дата | Развёртка стены В. Кухня-столовая (пом. 1) |
| Дизайнер | Кырлан А.С. | | | 19.10.26 | |

| Стадия | Лист | Листов |
|---|---|---|
| П | 57 | 156 |

выпуск 18.10.2026 № 8cd922c868 · стр. 57 из 156

Правка к этому листу

## Развёртка стены Г

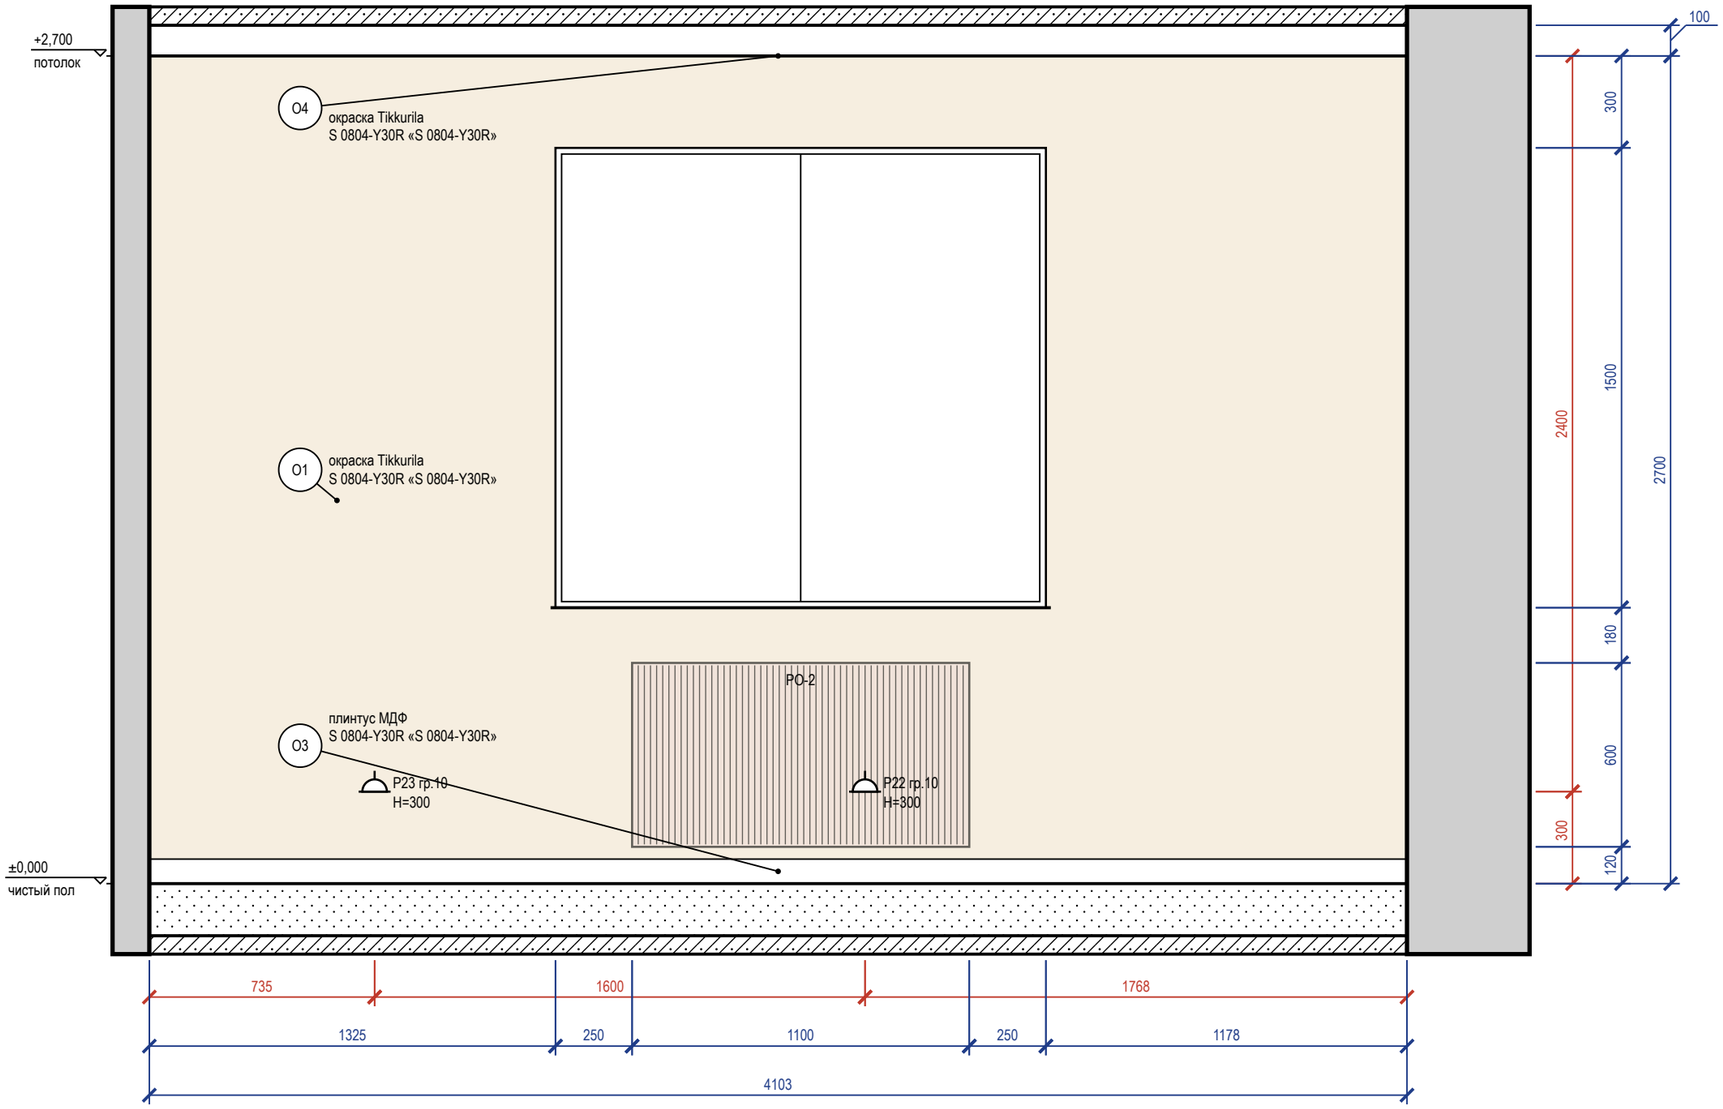


## Схема развёрток (М 1:100)

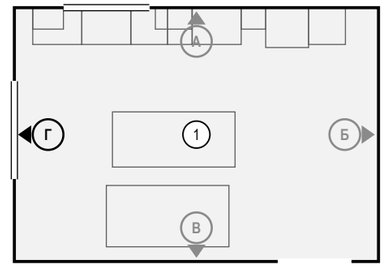


Визуализация этой стены — лист 54

## Ведомость отделки (на листе)

| Марка | Поверхность | Материал, изделие | Цвет, код | Кол. |
|---|---|---|---|---|
| О1 | стены | окраска, Tikkurila Luja 7, шелковисто-матовая, подготовка К3 | NCS S 0804-Y30R «S 0804-Y30R» | 8,7 м² |
| О3 | плинтус | плинтус МДФ, h 80 мм, аналог: плинтус МДФ под окраску 80×16 мм, полуглянцевая | NCS S 0804-Y30R «S 0804-Y30R» | 4,1 м |
| О4 | потолок | окраска, Tikkurila Luja 7, матовая, подготовка Q3 | NCS S 0804-Y30R «S 0804-Y30R» | 24,6 м² |

## Примечания

1. Размеры — в мм от чистовых поверхностей стен; условные обозначения и общие указания — лист 2.

| | | | | | |
|---|---|---|---|---|---|
| | | | | | Проект: Дом 331 м² |
| | Лист | № док. | Подпись | Дата | Развёртка стены Г. Кухня-столовая (пом. 1) |
| Дизайнер | Кырлан А.С. | | | 19.10.26 | |

| Стадия | Лист | Листов |
|---|---|---|
| П | 58 | 156 |

выпуск 18.10.2026 № 8cd922c868 · стр. 58 из 156

Правка к этому листу

| | | | | | | |
|---|---|---|---|---|---|---|
| | | | | | Проект: Дом 331 м² | |
| | Лист | № док. | Подпись | Дата | | |
| Дизайнер | Кырлан А.С. | | | 19.10.26 | Визуализация: Кабинет-гостевая | Стадия / Лист / Листов |
| | | | | | | П / 59 / 156 |

выпуск 18.10.2026 № 8cd922c868 · стр. 59 из 156

Правка к этому листу

| | | | | | | |
|---|---|---|---|---|---|---|
| | | | | | Проект: Дом 331 м² | |
| | Лист | № док. | Подпись | Дата | | |
| Дизайнер | Кырлан А.С. | | | 19.10.26 | Визуализация: Кабинет-гостевая | Стадия / Лист / Листов |
| | | | | | | П / 60 / 156 |

выпуск 18.10.2026 № 8cd922c868 · стр. 60 из 156

Правка к этому листу

## Развёртка стены А

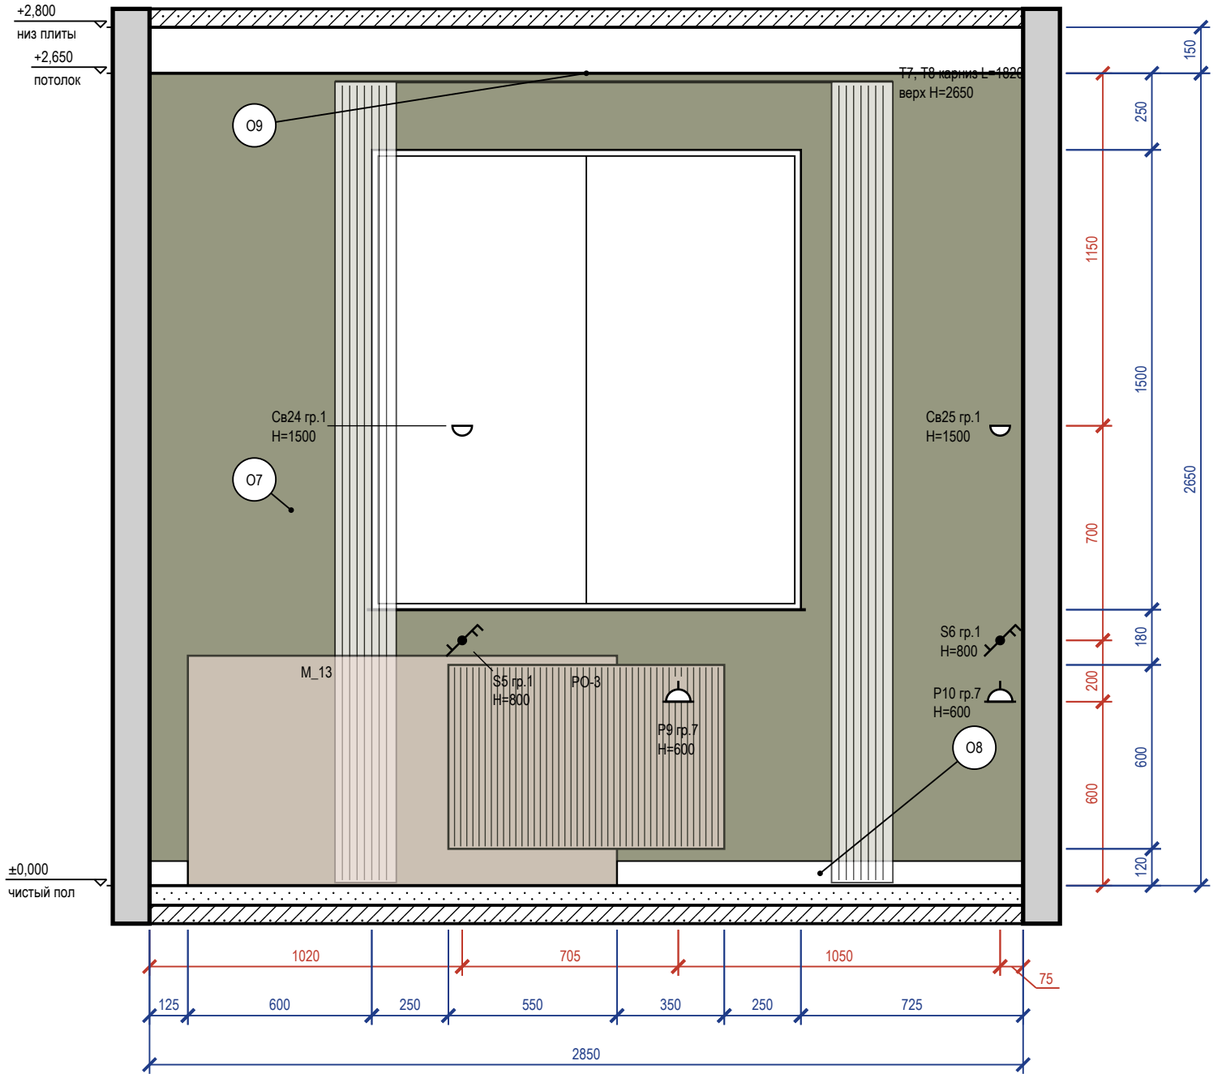


## Схема развёрток (М 1:100)

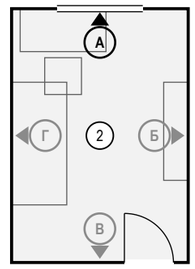


## Ведомость отделки (на листе)

| Марка | Поверхность | Материал, изделие | Цвет, код | Кол. |
|---|---|---|---|---|
| О7 | акцентная стена | окраска, Farrow & Ball Modern Emulsion, матовая, подготовка Q3 | Farrow & Ball No. 298 «Bancha» | 5,5 м² |
| О8 | плинтус | плинтус МДФ, h 80 мм, аналог: плинтус МДФ под покраску 80×16 | Farrow & Ball No. 226 «Joa's White» | 1,4 м |
| О9 | потолок | окраска, Tikkurila Anti-Reflex 2, глубокоматовая, подготовка Q3 | Little Greene No. 105 «Slaked Lime» | 11,9 м² |

Визуализация этой стены — лист 59

### Примечания

1. Размеры — в мм от чистовых поверхностей стен; условные обозначения и общие указания — лист 2.
2. Карнизы (шины) — по ведомости текстиля декоратора; длина L и верх Н — по развёртке, крепление — до окраски потолка.
3. Потолок на развёртках — по нижнему уровню У1; другие уровни потолка помещения: У2 +2,700.
4. Линии узора (швы плитки, складки штор, рёбра радиаторов) прерываются у знаков и выносок — просвет между линиями не менее 0,7 мм.

| | | | | | |
|---|---|---|---|---|---|
| | | | | | Проект: Дом 331 м² |
| | Лист | № док. | Подпись | Дата | Развёртка стены А. Кабинет-гостевая (пом. 2) |
| Дизайнер | Кырлан А.С. | | | 19.10.26 | |

| Стадия | Лист | Листов |
|---|---|---|
| П | 61 | 156 |

выпуск 18.10.2026 № 8cd922c868 · стр. 61 из 156

Правка к этому листу

## Развёртка стены Б

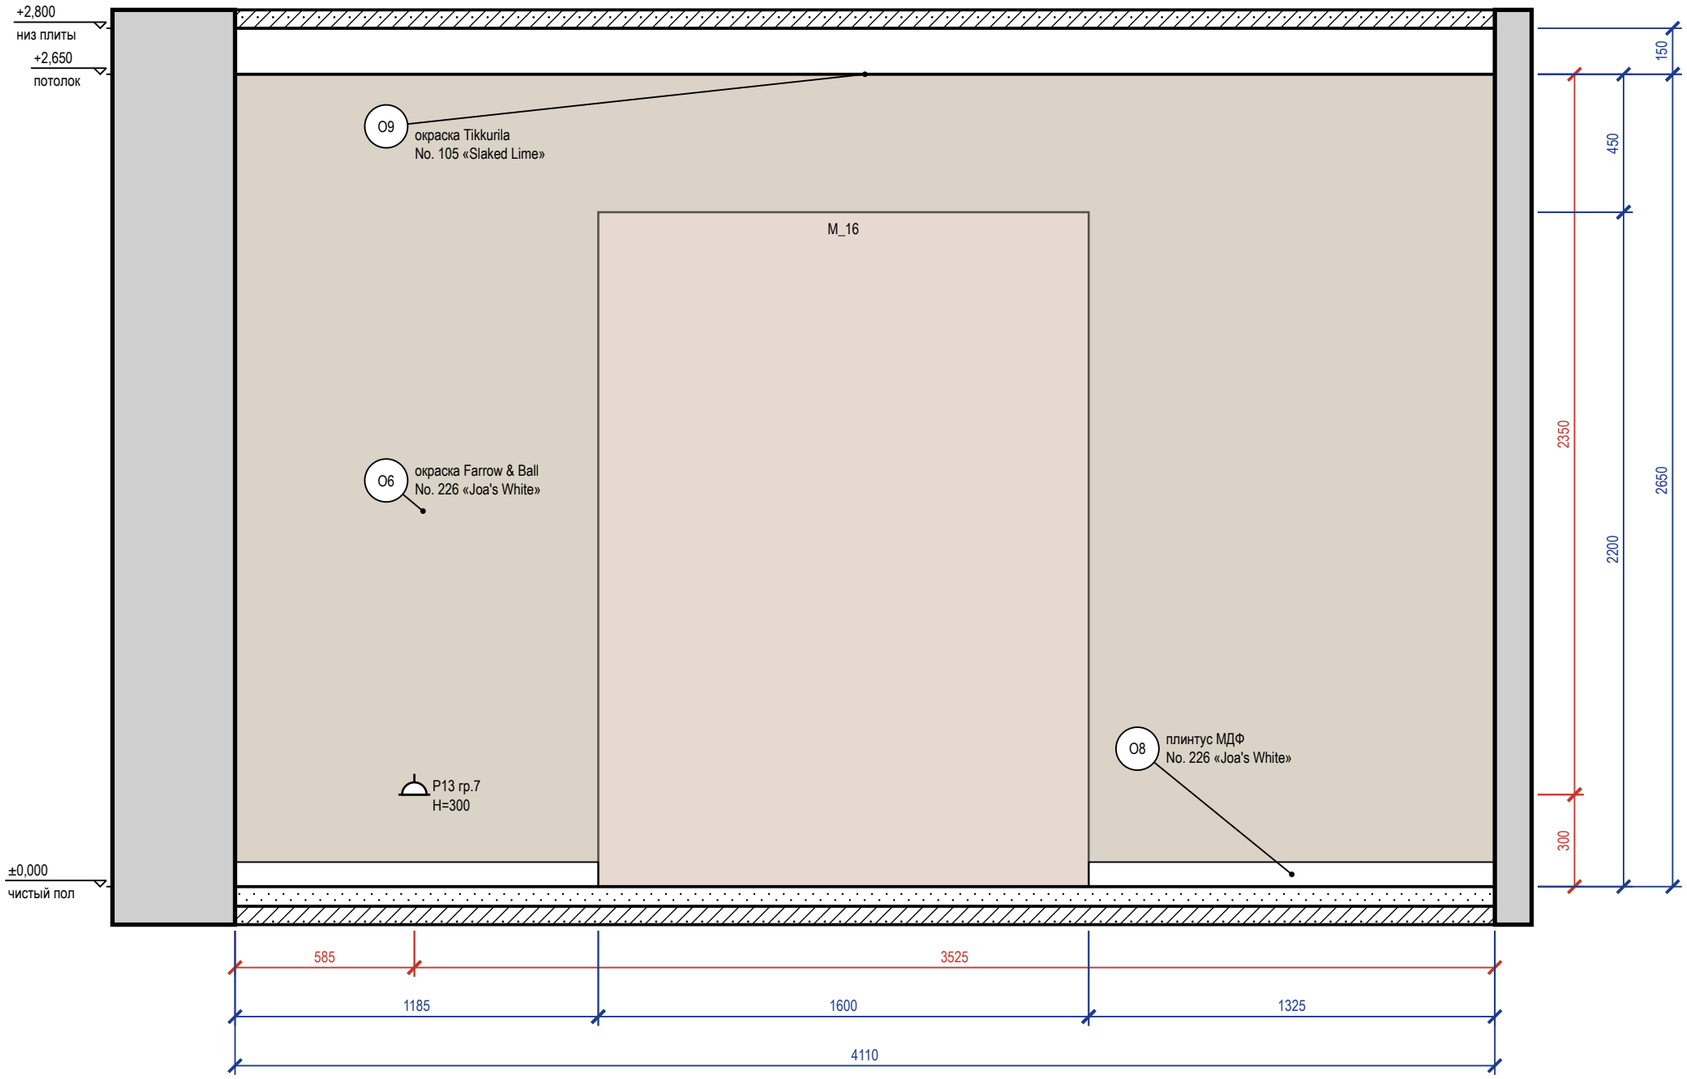


## Схема развёрток (М 1:100)

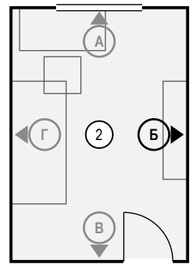


Визуализация этой стены

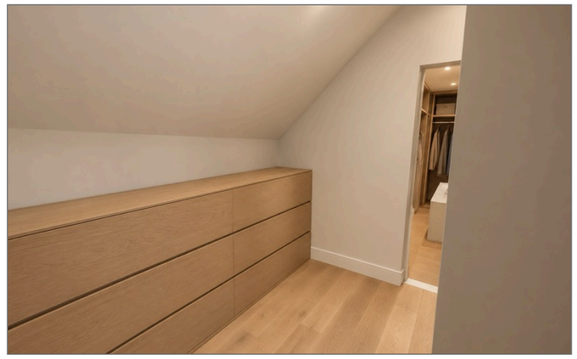

## Ведомость отделки (на листе)

| Марка | Поверхность | Материал, изделие | Цвет, код | Кол. |
|---|---|---|---|---|
| О6 | стены | окраска, Farrow & Ball Modern Emulsion, матовая, подготовка Q3 | Farrow & Ball No. 226 «Joa's White» | 10,9 м² |
| О8 | плинтус | плинтус МДФ, h 80 мм, аналог: плинтус МДФ под покраску 80×16 | Farrow & Ball No. 226 «Joa's White» | 2,5 м |
| О9 | потолок | окраска, Tikkurila Anti-Reflex 2, глубокоматовая, подготовка Q3 | Little Greene No. 105 «Slaked Lime» | 11,9 м² |

## Примечания

1. Размеры — в мм от чистовых поверхностей стен; условные обозначения и общие указания — лист 2.
2. Потолок на развёртках — по нижнему уровню У1; другие уровни потолка помещения: У2 +2,700.

| | | | | | |
|---|---|---|---|---|---|
| | | | | | Проект: Дом 331 м² |
| | Лист | № док. | Подпись | Дата | Развёртка стены Б. Кабинет-гостевая (пом. 2) |
| Дизайнер | Кырлан А.С. | | | 19.10.26 | |

| Стадия | Лист | Листов |
|---|---|---|
| П | 62 | 156 |

выпуск 18.10.2026 № 8cd922c868 · стр. 62 из 156

Правка к этому листу

## Развёртка стены В

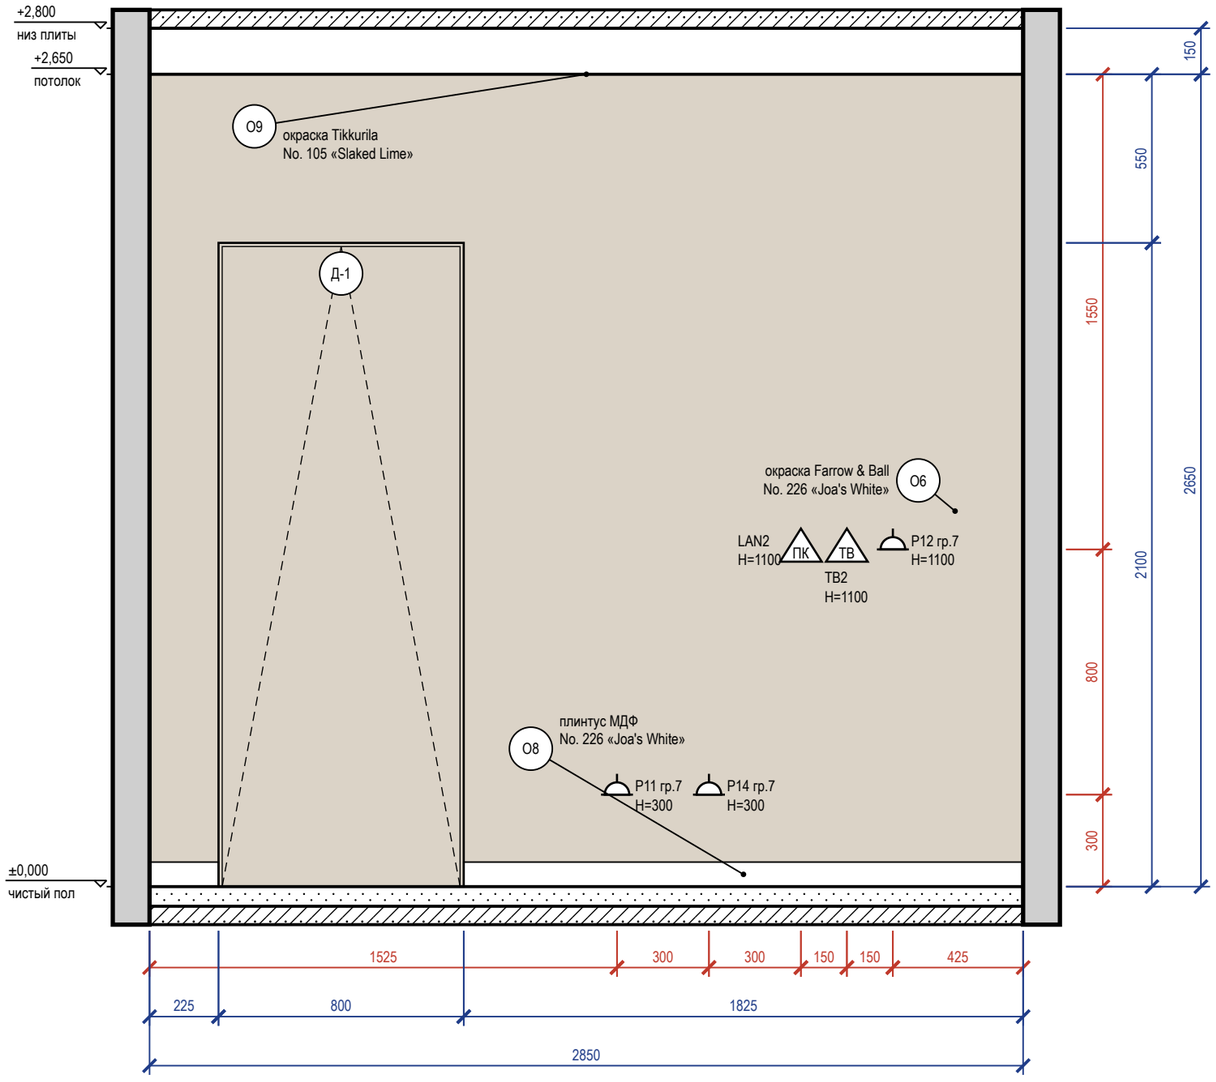


## Схема развёрток (М 1:100)

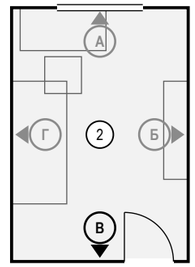


## Ведомость отделки (на листе)

| Марка | Поверхность | Материал, изделие | Цвет, код | Кол. |
|---|---|---|---|---|
| О6 | стены | окраска, Farrow & Ball Modern Emulsion, матовая, подготовка Q3 | Farrow & Ball No. 226 «Joa's White» | 5,9 м² |
| О8 | плинтус | плинтус МДФ, h 80 мм, аналог: плинтус МДФ под покраску 80×16 | Farrow & Ball No. 226 «Joa's White» | 2 м |
| О9 | потолок | окраска, Tikkurila Anti-Reflex 2, глубокоматовая, подготовка Q3 | Little Greene No. 105 «Slaked Lime» | 11,9 м² |

## Примечания

1. Размеры — в мм от чистовых поверхностей стен; условные обозначения и общие указания — лист 2.
2. Двери скрытого монтажа — полотно в плоскости стены, отделка стены по полотну, плинтус прерывается у короба (узел — на листе узлов).
3. Потолок на развёртках — по нижнему уровню У1; другие уровни потолка помещения: У2 +2,700.

| | | | | | |
|---|---|---|---|---|---|
| | | | | | Проект: Дом 331 м² |
| | Лист | № док. | Подпись | Дата | Развёртка стены В. Кабинет-гостевая (пом. 2) |
| Дизайнер | Кырлан А.С. | | | 19.10.26 | |

| Стадия | Лист | Листов |
|---|---|---|
| П | 63 | 156 |

выпуск 18.10.2026 № 8cd922c868 · стр. 63 из 156

Правка к этому листу

## Развёртка стены Г

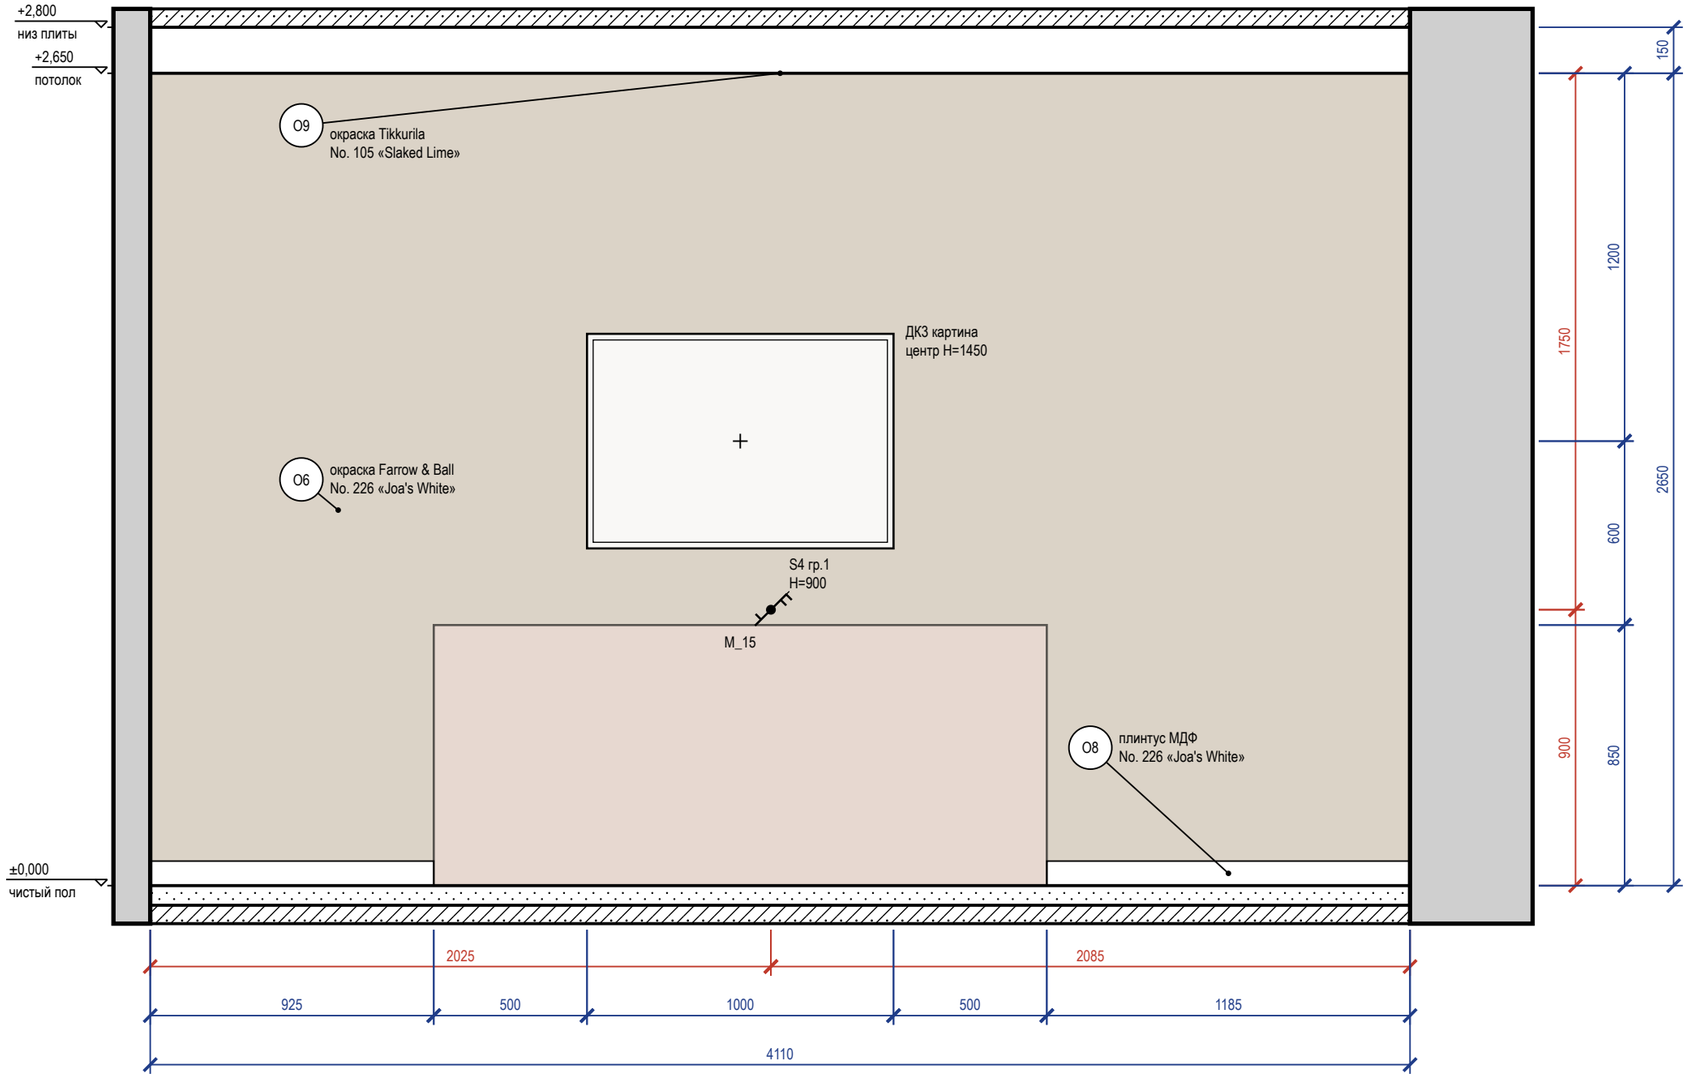


## Схема развёрток (М 1:100)

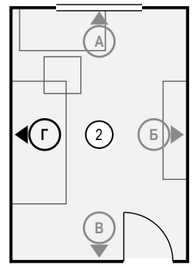


Визуализация этой стены — лист 60

### Ведомость отделки (на листе)

| Марка | Поверхность | Материал, изделие | Цвет, код | Кол. |
|---|---|---|---|---|
| О6 | стены | окраска, Farrow & Ball Modern Emulsion, матовая, подготовка Q3 | Farrow & Ball No. 226 «Joa's White» | 10,9 м² |
| О8 | плинтус | плинтус МДФ, h 80 мм, аналог: плинтус МДФ под покраску 80×16 | Farrow & Ball No. 226 «Joa's White» | 2,1 м |
| О9 | потолок | окраска, Tikkurila Anti-Reflex 2, глубокоматовая, подготовка Q3 | Little Greene No. 105 «Slaked Lime» | 11,9 м² |

### Примечания

1. Размеры — в мм от чистовых поверхностей стен; условные обозначения и общие указания — лист 2.
2. Картины и зеркала крепить к основанию по паспорту изделия (закладные и анкеры — в перечне скрытых работ); крест — ось центра предмета.
3. Потолок на развёртках — по нижнему уровню У1; другие уровни потолка помещения: У2 +2,700.

| | | | | | |
|---|---|---|---|---|---|
| | | | | | Проект: Дом 331 м² |
| | Лист | № док. | Подпись | Дата | Развёртка стены Г. Кабинет-гостевая (пом. 2) |
| Дизайнер | Кырлан А.С. | | | 19.10.26 | |

| Стадия | Лист | Листов |
|---|---|---|
| П | 64 | 156 |

выпуск 18.10.2026 № 8cd922c868 · стр. 64 из 156

Правка к этому листу

| | | | | | Проект: Дом 331 м² | | | |
|---|---|---|---|---|---|---|---|---|
| | Лист | № док. | Подпись | Дата | Визуализация: Санузел 1 этажа | Стадия | Лист | Листов |
| Дизайнер | Кырлан А.С. | | | 19.10.26 | | П | 65 | 156 |

выпуск 18.10.2026 № 8cd922c868 · стр. 65 из 156

Правка к этому листу

## Развёртка стены А

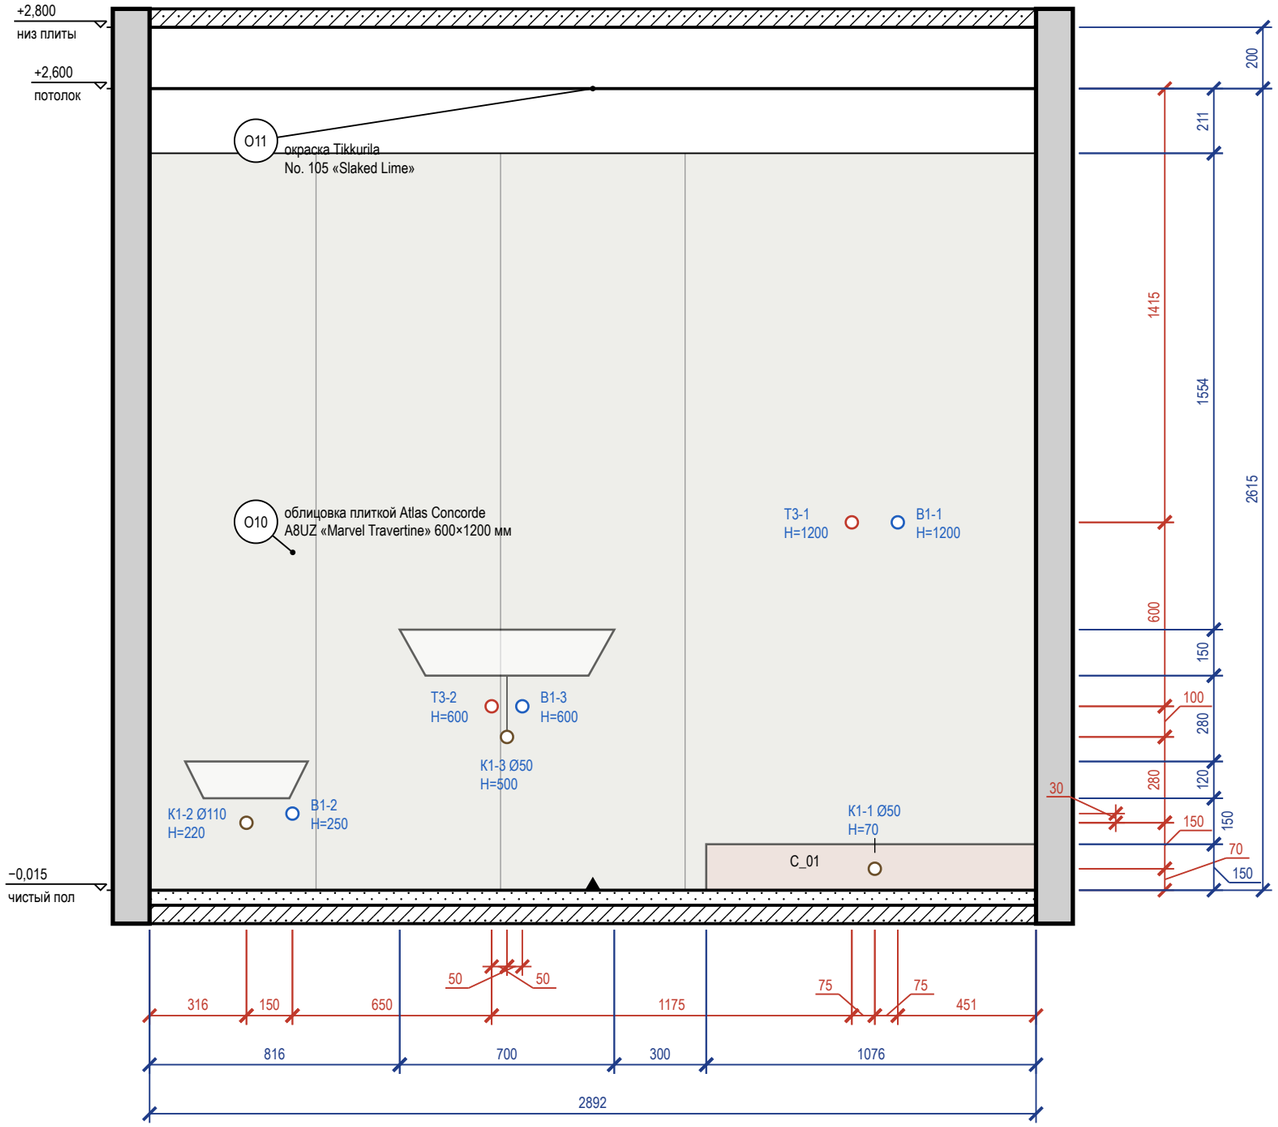


## Схема развёрток (М 1:100)

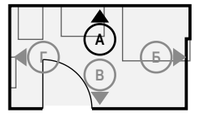


## Ведомость отделки (на листе)

| Марка | Поверхность | Материал, изделие | Цвет, код | Кол. |
|---|---|---|---|---|
| О10 | стены | облицовка плиткой, Atlas Concorde Marvel Travertine, 600×1200×9 мм, A8UZ, затирка CG2WA | Atlas Concorde A8UZ «Marvel Travertine» | 7 м² |
| О11 | потолок | окраска, Tikkurila Luja 7, матовая, подготовка Q3 | Little Greene No. 105 «Slaked Lime» | 4,9 м² |

Визуализация этой стены

## Примечания

1. Размеры — в мм от чистовых поверхностей стен; условные обозначения и общие указания — лист 2.
2. Схема мебели, приборов и декора не является технической документацией для производства мебели; габариты — по паспортам изделий.
3. Выводы ВК — коды и высоты по листу выводов сантехники.
4. Облицовка — по сетке швов 2 мм, раскладка от оси стены (треугольник у пола), целые ряды от пола; подрезки — по листу раскладки плитки.
5. Гидроизоляция в 2 слоя, заход на стены 200 мм — до облицовки, с актом скрытых работ и тестом проливом (узел — на листе узлов).

| | | | | | |
|---|---|---|---|---|---|
| | | | | | Проект: Дом 331 м² |
| | Лист | № док. | Подпись | Дата | Развёртка стены А. Санузел 1 этажа (пом. 3) |
| Дизайнер | Кырлан А.С. | | | 19.10.26 | |

| Стадия | Лист | Листов |
|---|---|---|
| П | 66 | 156 |

выпуск 18.10.2026 № 8cd922c868 · стр. 66 из 156

Правка к этому листу

## Развёртка стены Б

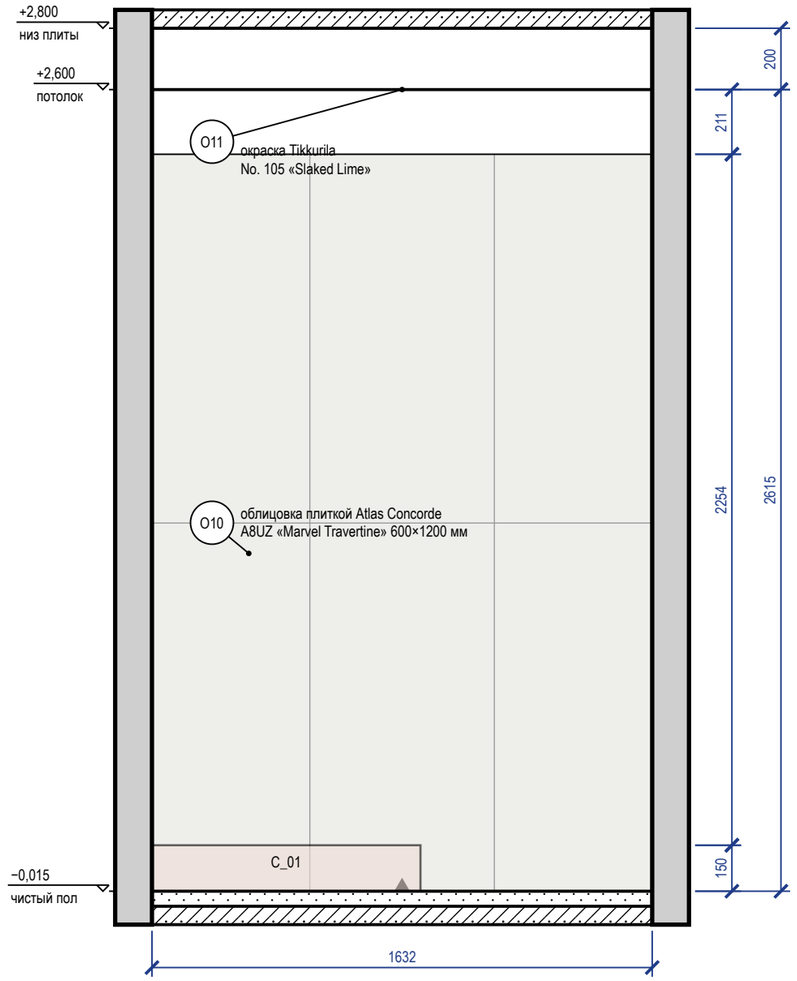


## Развёртка стены В

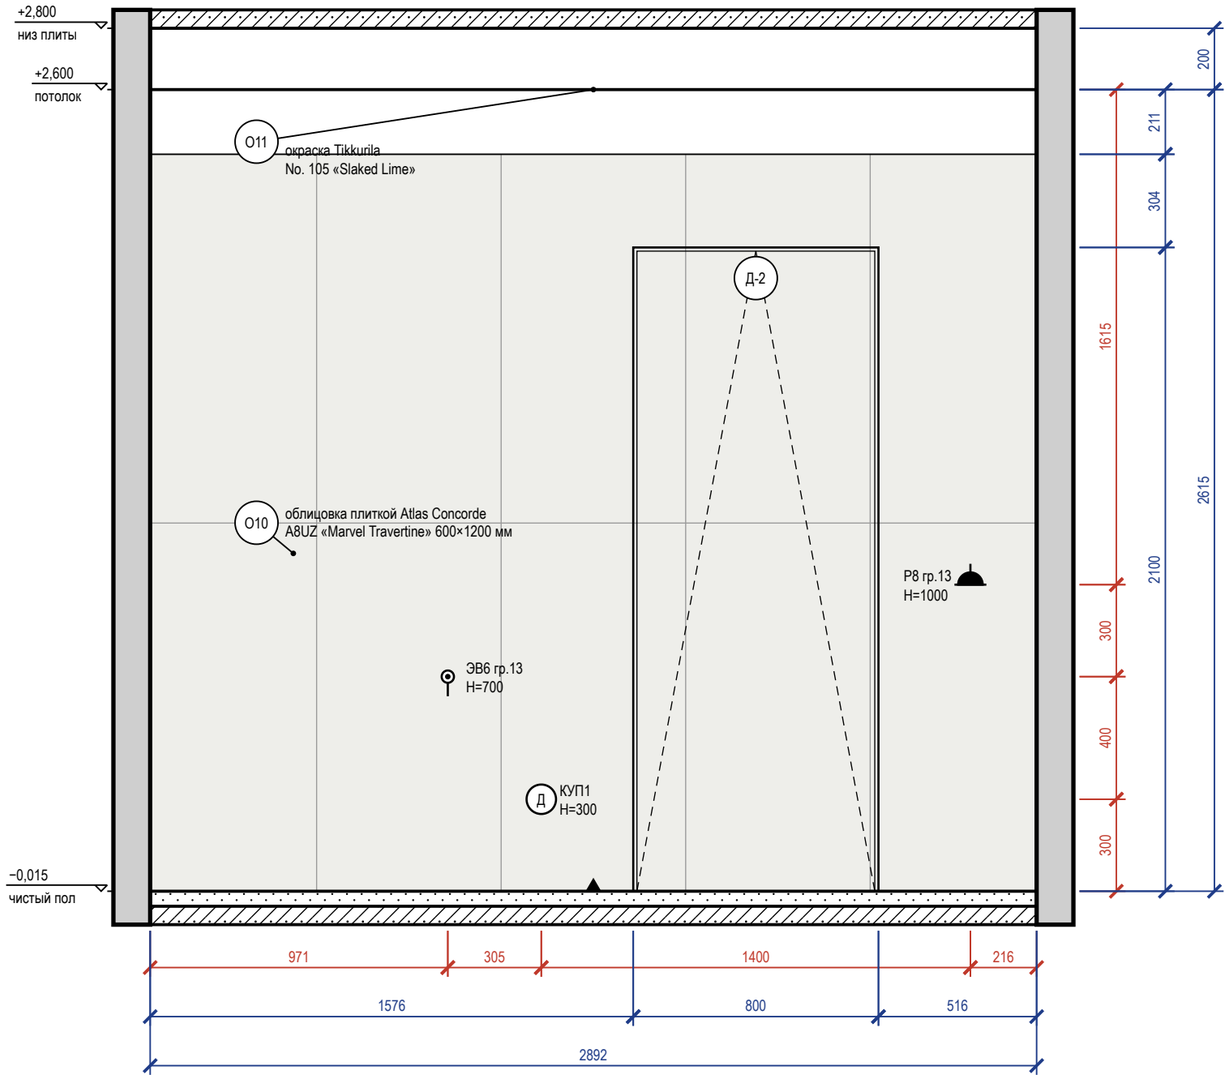


### Схема развёрток (М 1:100)

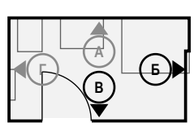


### Ведомость отделки (на листе)

| Марка | Поверхность | Материал, изделие | Цвет, код | Кол. |
|---|---|---|---|---|
| О10 | стены | облицовка плиткой, Atlas Concorde Marvel Travertine, 600×1200×9 мм, A8UZ, затирка CG2WA | Atlas Concorde A8UZ «Marvel Travertine» | 9,2 м² |
| О11 | потолок | окраска, Tikkurila Luja 7, матовая, подготовка Q3 | Little Greene No. 105 «Slaked Lime» | 4,9 м² |

Визуализация этой стены — лист 65

### Примечания

1. Размеры — в мм от чистовых поверхностей стен; условные обозначения и общие указания — лист 2.
2. Схема мебели, приборов и декора не является технической документацией для производства мебели; габариты — по паспортам изделий.
3. Облицовка — по сетке швов 2 мм, раскладка от оси стены (треугольник у пола), целые ряды от пола; подрезки — по листу раскладки плитки.
4. Гидроизоляция в 2 слоя, заход на стены 200 мм — до облицовки, с актом скрытых работ и тестом проливом (узел — на листе узлов).
5. Двери скрытого монтажа — полотно в плоскости стены, отделка стены по полотну, плинтус прерывается у короба (узел — на листе узлов).

| | | | | | |
|---|---|---|---|---|---|
| | | | | | Проект: Дом 331 м² |
| | Лист | № док. | Подпись | Дата | Развёртки стен Б, В. Санузел 1 этажа (пом. 3) |
| Дизайнер | Кырлан А.С. | | | 19.10.26 | |

| Стадия | Лист | Листов |
|---|---|---|
| П | 67 | 156 |

выпуск 18.10.2026 № 8cd922c868 · стр. 67 из 156

## Развёртка стены Г

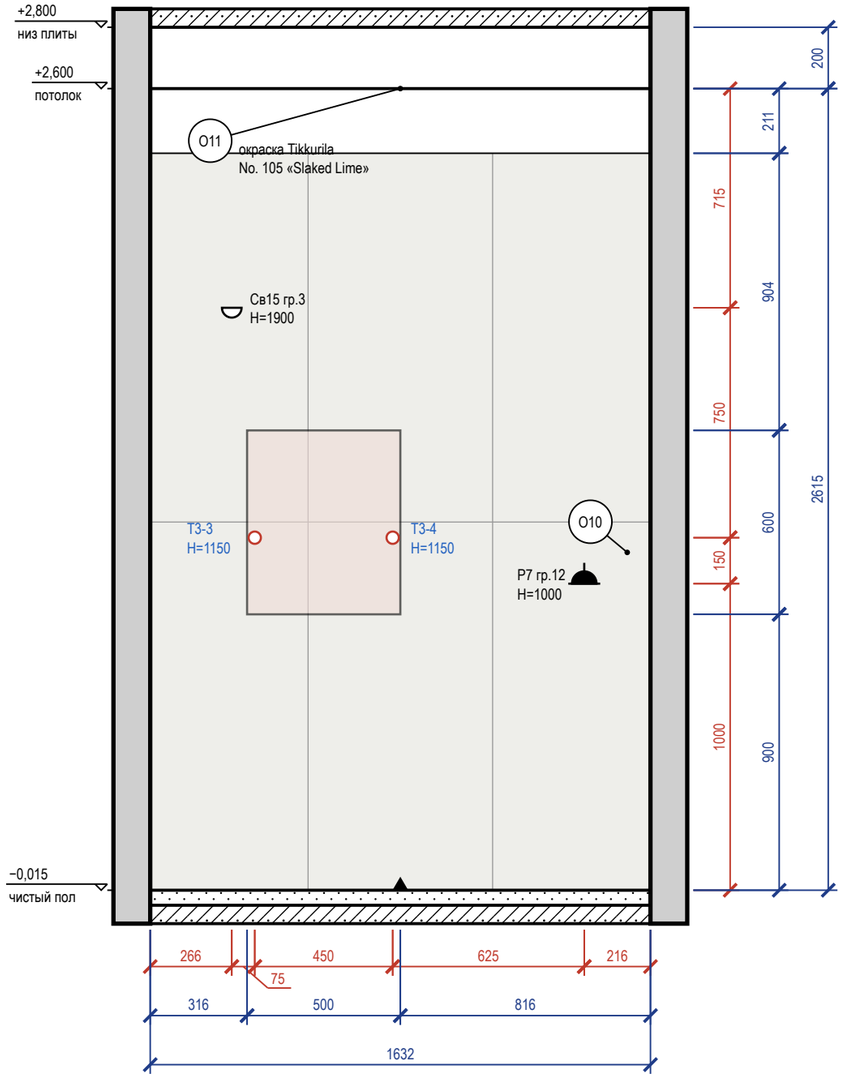


## Схема развёрток (М 1:100)

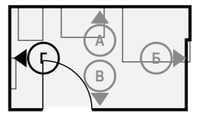


## Ведомость отделки (на листе)

| Марка | Поверхность | Материал, изделие | Цвет, код | Кол. |
|---|---|---|---|---|
| О10 | стены | облицовка плиткой, Atlas Concorde Marvel Travertine, 600×1200×9 мм, A8UZ, затирка CG2WA | Atlas Concorde A8UZ «Marvel Travertine» | 3,9 м² |
| О11 | потолок | окраска, Tikkurila Luja 7, матовая, подготовка Q3 | Little Greene No. 105 «Slaked Lime» | 4,9 м² |

## Примечания

1. Размеры — в мм от чистовых поверхностей стен; условные обозначения и общие указания — лист 2.
2. Схема мебели, приборов и декора не является технической документацией для производства мебели; габариты — по паспортам изделий.
3. Выводы ВК — коды и высоты по листу выводов сантехники.
4. Облицовка — по сетке швов 2 мм, раскладка от оси стены (треугольник у пола), целые ряды от пола; подрезки — по листу раскладки плитки.
5. Гидроизоляция в 2 слоя, заход на стены 200 мм — до облицовки, с актом скрытых работ и тестом проливом (узел — на листе узлов).

| | | | | | |
|---|---|---|---|---|---|
| | | | | | Проект: Дом 331 м² |
| | Лист | № док. | Подпись | Дата | Развёртка стены Г. Санузел 1 этажа (пом. 3) |
| Дизайнер | Кырлан А.С. | | | 19.10.26 | |

| Стадия | Лист | Листов |
|---|---|---|
| П | 68 | 156 |

Правка к этому листу

| | | | | | |
|---|---|---|---|---|---|
| | | | | | Проект: Дом 331 м² |
| | Лист | № док. | Подпись | Дата | |
| Дизайнер | Кырлан А.С. | | | 19.10.26 | Визуализация: Котельная |

| Стадия | Лист | Листов |
|---|---|---|
| П | 69 | 156 |

выпуск 18.10.2026 № 8cd922c868 · стр. 69 из 156

Правка к этому листу

## Развёртка стены А

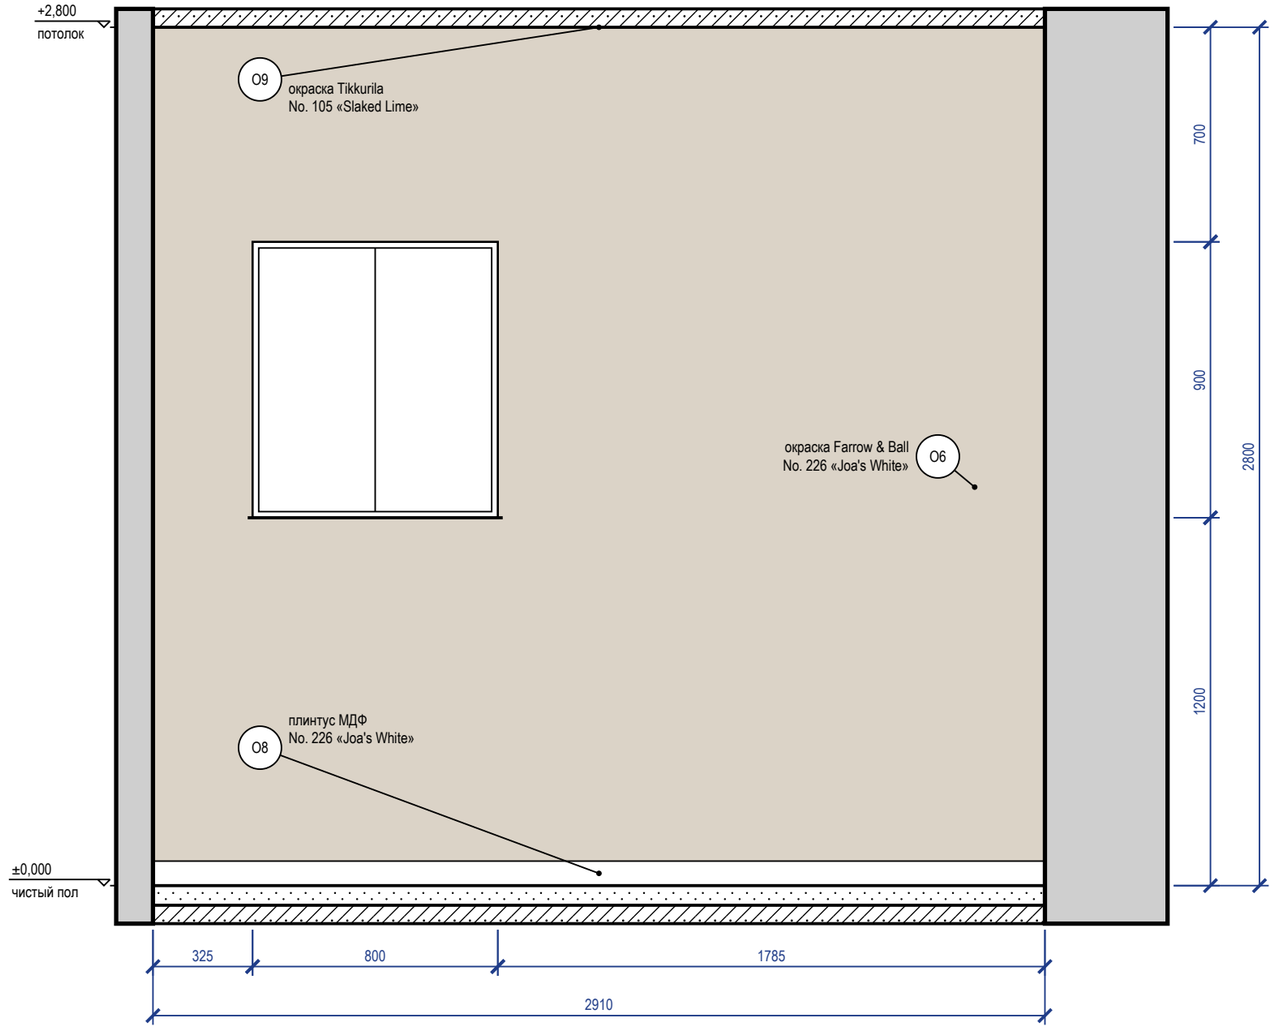


## Схема развёрток (М 1:100)

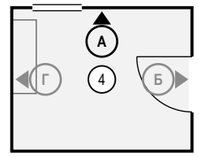


## Ведомость отделки (на листе)

| Марка | Поверхность | Материал, изделие | Цвет, код | Кол. |
|---|---|---|---|---|
| О6 | стены | окраска, Farrow & Ball Modern Emulsion, матовая, подготовка Q3 | Farrow & Ball No. 226 «Joa's White» | 7,4 м² |
| О8 | плинтус | плинтус МДФ, h 80 мм, аналог: плинтус МДФ под покраску 80×16 | Farrow & Ball No. 226 «Joa's White» | 2,9 м |
| О9 | потолок | окраска, Tikkurila Anti-Reflex 2, глубокоматовая, подготовка Q3 | Little Greene No. 105 «Slaked Lime» | 6,9 м² |

## Примечания

1. Размеры — в мм от чистовых поверхностей стен; условные обозначения и общие указания — лист 2.

| | | | | | |
|---|---|---|---|---|---|
| | | | | | Проект: Дом 331 м² |
| | Лист | № док. | Подпись | Дата | Развёртка стены А. Котельная (пом. 4) |
| Дизайнер | Кырлан А.С. | | | 19.10.26 | |

| Стадия | Лист | Листов |
|---|---|---|
| П | 70 | 156 |

выпуск 18.10.2026 № 8cd922c868 · стр. 70 из 156

Правка к этому листу

## Развёртка стены Б

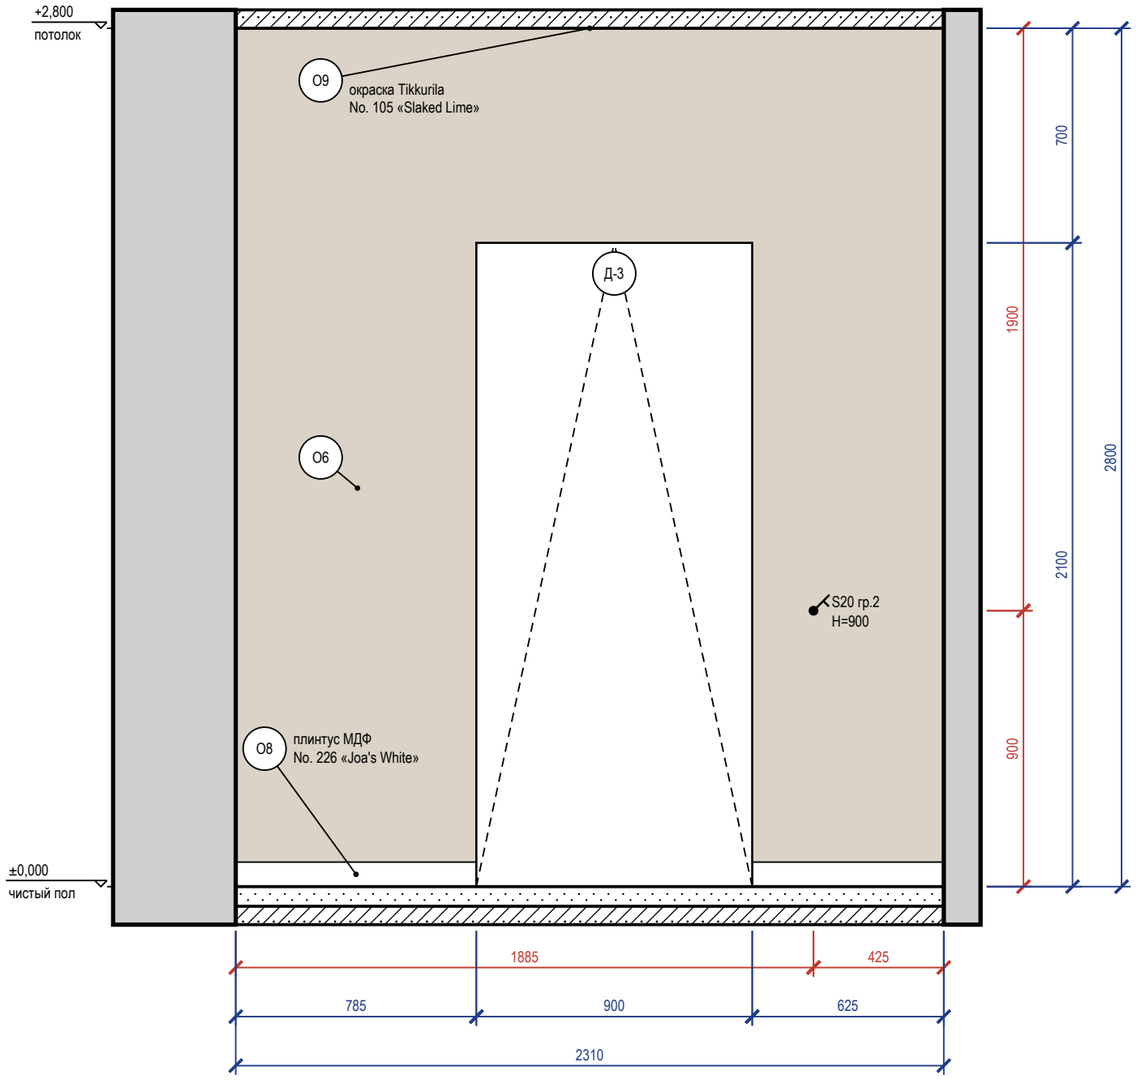


## Развёртка стены Г

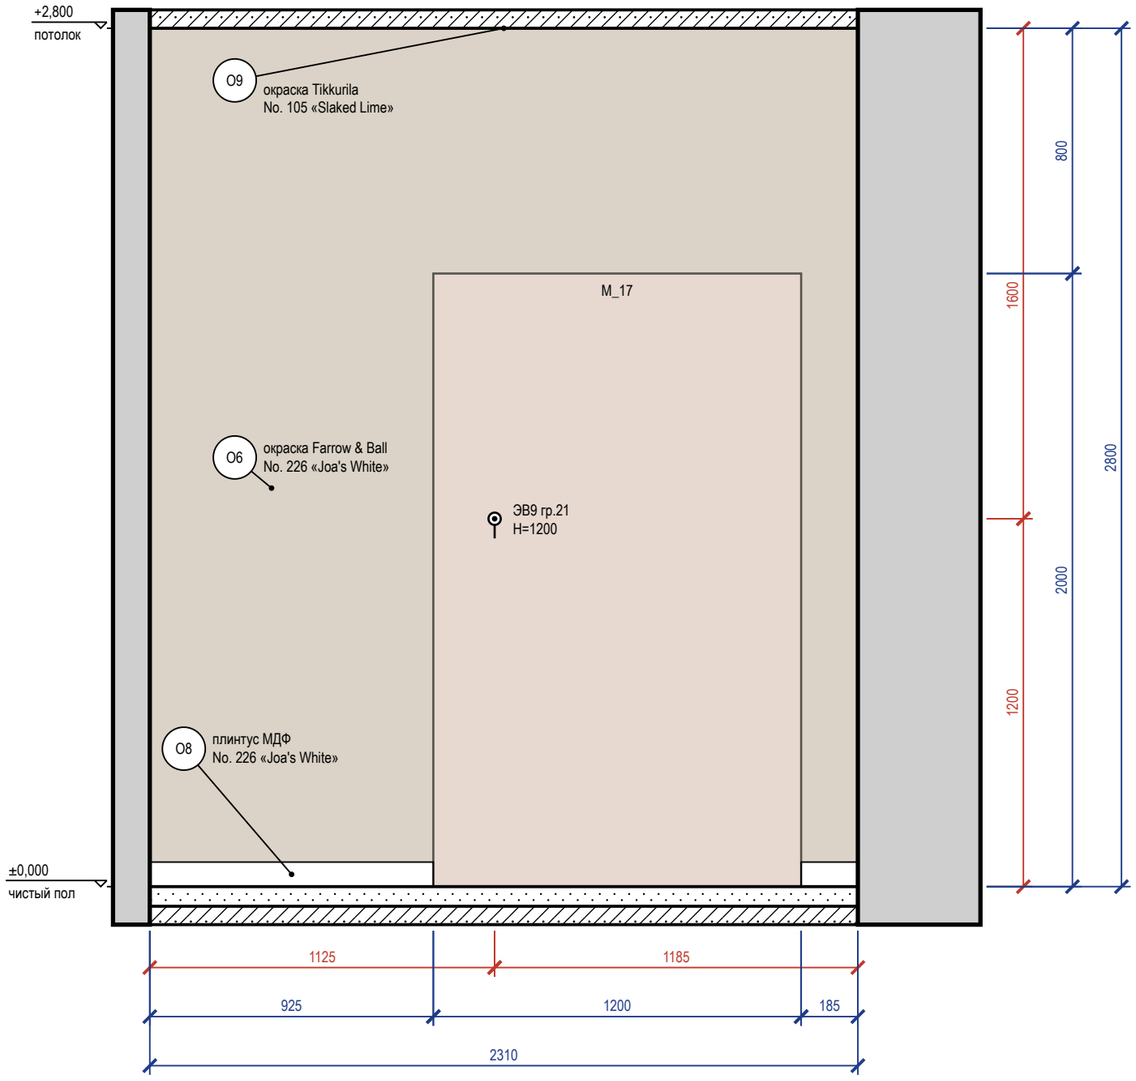


### Схема развёрток (М 1:100)

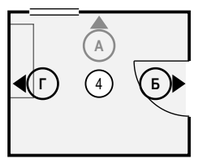


### Ведомость отделки (на листе)

| Марка | Поверхность | Материал, изделие | Цвет, код | Кол. |
|---|---|---|---|---|
| О6 | стены | окраска, Farrow & Ball Modern Emulsion, матовая, подготовка Q3 | Farrow & Ball No. 226 «Joa's White» | 11 м² |
| О8 | плинтус | плинтус МДФ, h 80 мм, аналог: плинтус МДФ под покраску 80×16 | Farrow & Ball No. 226 «Joa's White» | 2,5 м |
| О9 | потолок | окраска, Tikkurila Anti-Reflex 2, глубокоматовая, подготовка Q3 | Little Greene No. 105 «Slaked Lime» | 6,9 м² |

Визуализация этой стены

### Примечания

1. Размеры — в мм от чистовых поверхностей стен; условные обозначения и общие указания — лист 2.

| | | | | | |
|---|---|---|---|---|---|
| | Лист | № док. | Подпись | Дата | Проект: Дом 331 м² |
| Дизайнер | Кырлан А.С. | | | 19.10.26 | Развёртки стен Б, Г. Котельная (пом. 4) |

| Стадия | Лист | Листов |
|---|---|---|
| П | 71 | 156 |

выпуск 18.10.2026 № 8cd922c868 · стр. 71 из 156

Правка к этому листу

| | | | | | |
|---|---|---|---|---|---|
| | | | | | Проект: Дом 331 м² |
| | Лист | № док. | Подпись | Дата | Визуализация гостиной |
| Дизайнер | Кырлан А.С. | | | 19.10.26 | |

| Стадия | Лист | Листов |
|---|---|---|
| П | 72 | 156 |

выпуск 18.10.2026 № 8cd922c868 · стр. 72 из 156

Правка к этому листу

| | | | | | Проект: Дом 331 м² | | | |
|---|---|---|---|---|---|---|---|---|
| | Лист | № док. | Подпись | Дата | | | | |
| Дизайнер | Кырлан А.С. | | | 19.10.26 | Визуализация гостиной | Стадия | Лист | Листов |
| | | | | | | П | 73 | 156 |

выпуск 18.10.2026 № 8cd922c868 · стр. 73 из 156

Правка к этому листу

| | | | | | |
|---|---|---|---|---|---|
| | | | | | Проект: Дом 331 м² |
| | Лист | № док. | Подпись | Дата | |
| Дизайнер | Кырлан А.С. | | | 19.10.26 | Визуализация гостиной |

| Стадия | Лист | Листов |
|---|---|---|
| П | 74 | 156 |

выпуск 18.10.2026 № 8cd922c868 · стр. 74 из 156

Правка к этому листу

## Развёртка стены А

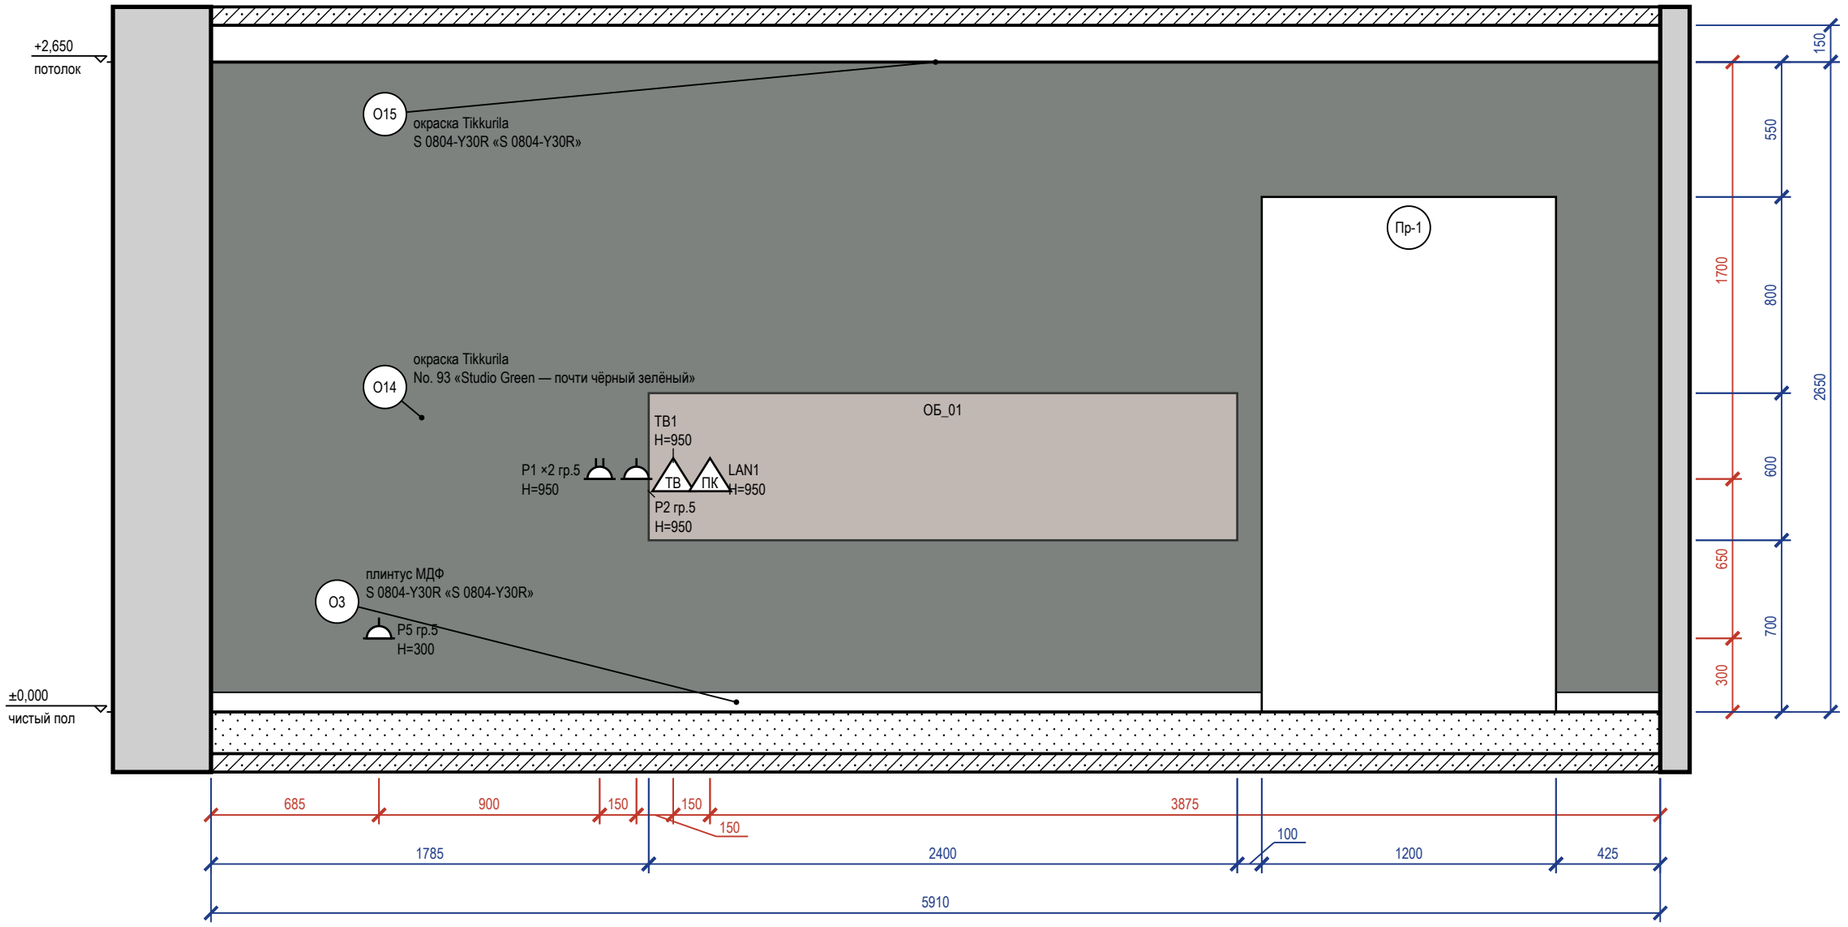


### Схема развёрток (М 1:100)

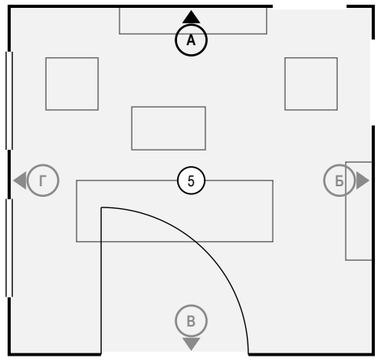


### Ведомость отделки (на листе)

| Марка | Поверхность | Материал, изделие | Цвет, код | Кол. |
|---|---|---|---|---|
| О3 | плинтус | плинтус МДФ, h 80 мм, аналог: плинтус МДФ под окраску 80×16 мм, полуглянцевая | NCS S 0804-Y30R «S 0804-Y30R» | 4,7 м |
| О14 | акцентная стена | окраска, Tikkurila Optiva 5 Matt, аналог: интерьерная краска, класс 2 по EN 13300, глубокоматовая/матовая, база С, матовая, подготовка К3 | Farrow & Ball No. 93 «Studio Green — почти чёрный зелёный» | 13,1 м² |
| О15 | потолок | окраска, Tikkurila Anti-Reflex 2, глубокоматовая, подготовка Q3 | NCS S 0804-Y30R «S 0804-Y30R» | 33,7 м² |

Визуализация этой стены — лист 72

### Примечания

1. Размеры — в мм от чистовых поверхностей стен; условные обозначения и общие указания — лист 2.
2. Схема мебели, приборов и декора не является технической документацией для производства мебели; габариты — по паспортам изделий.
3. Потолок на развёртках — по нижнему уровню У1; другие уровни потолка помещения: У2 +2,700.

| | | | | | |
|---|---|---|---|---|---|
| | | | | | Проект: Дом 331 м² |
| | Лист | № док. | Подпись | Дата | Развёртка стены А. Гостиная (пом. 5) |
| Дизайнер | Кырлан А.С. | | | 19.10.26 | |

| Стадия | Лист | Листов |
|---|---|---|
| П | 75 | 156 |

выпуск 18.10.2026 № 8cd922c868 · стр. 75 из 156

Правка к этому листу

## Развёртка стены Б

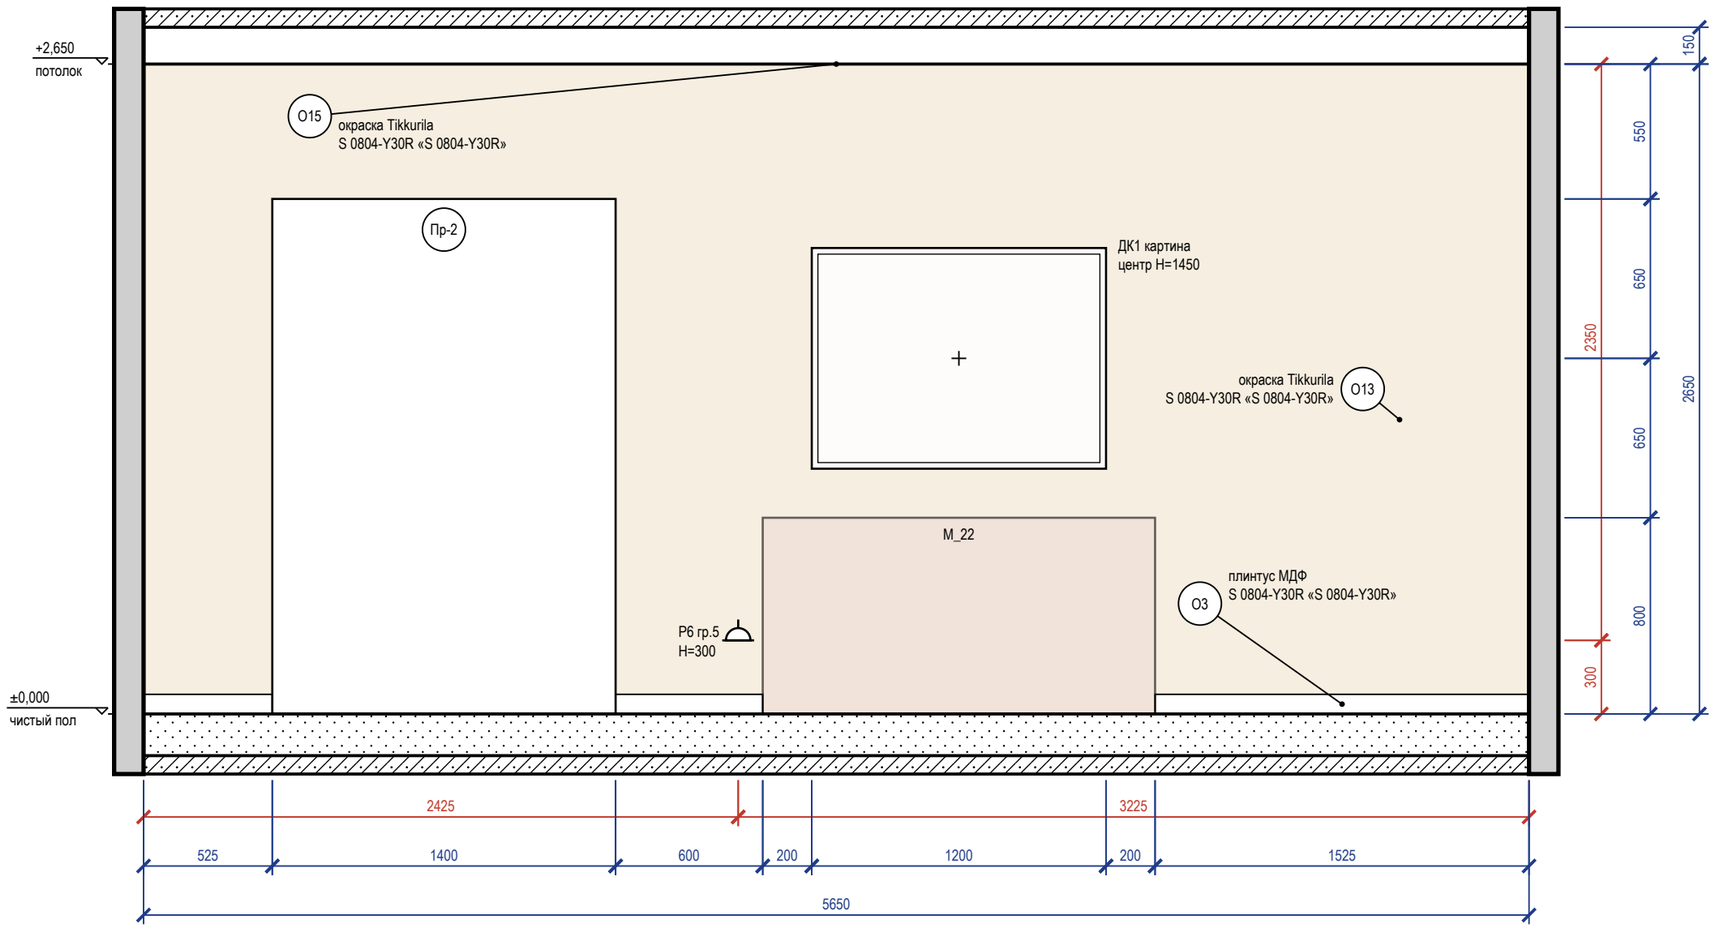


### Схема развёрток (М 1:100)

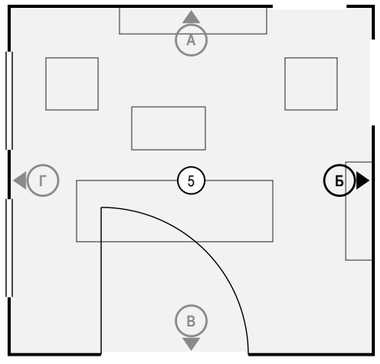


### Ведомость отделки (на листе)

| Марка | Поверхность | Материал, изделие | Цвет, код | Кол. |
|---|---|---|---|---|
| О3 | плинтус | плинтус МДФ, h 80 мм, аналог: плинтус МДФ под окраску 80×16 мм, полуглянцевая | NCS S 0804-Y30R «S 0804-Y30R» | 2,6 м |
| О13 | стены | окраска, Tikkurila Optiva 5 Matt, матовая, подготовка К3 | NCS S 0804-Y30R «S 0804-Y30R» | 12 м² |
| О15 | потолок | окраска, Tikkurila Anti-Reflex 2, глубокоматовая, подготовка Q3 | NCS S 0804-Y30R «S 0804-Y30R» | 33,7 м² |

### Примечания

1. Размеры — в мм от чистовых поверхностей стен; условные обозначения и общие указания — лист 2.
2. Картины и зеркала крепить к основанию по паспорту изделия (закладные и анкеры — в перечне скрытых работ); крест — ось центра предмета.
3. Потолок на развёртках — по нижнему уровню У1; другие уровни потолка помещения: У2 +2,700.

| | | | | | |
|---|---|---|---|---|---|
| | | | | | Проект: Дом 331 м² |
| | Лист | № док. | Подпись | Дата | Развёртка стены Б. Гостиная (пом. 5) |
| Дизайнер | Кырлан А.С. | | | 19.10.26 | |

| Стадия | Лист | Листов |
|---|---|---|
| П | 76 | 156 |

выпуск 18.10.2026 № 8cd922c868 · стр. 76 из 156

Правка к этому листу

## Развёртка стены В

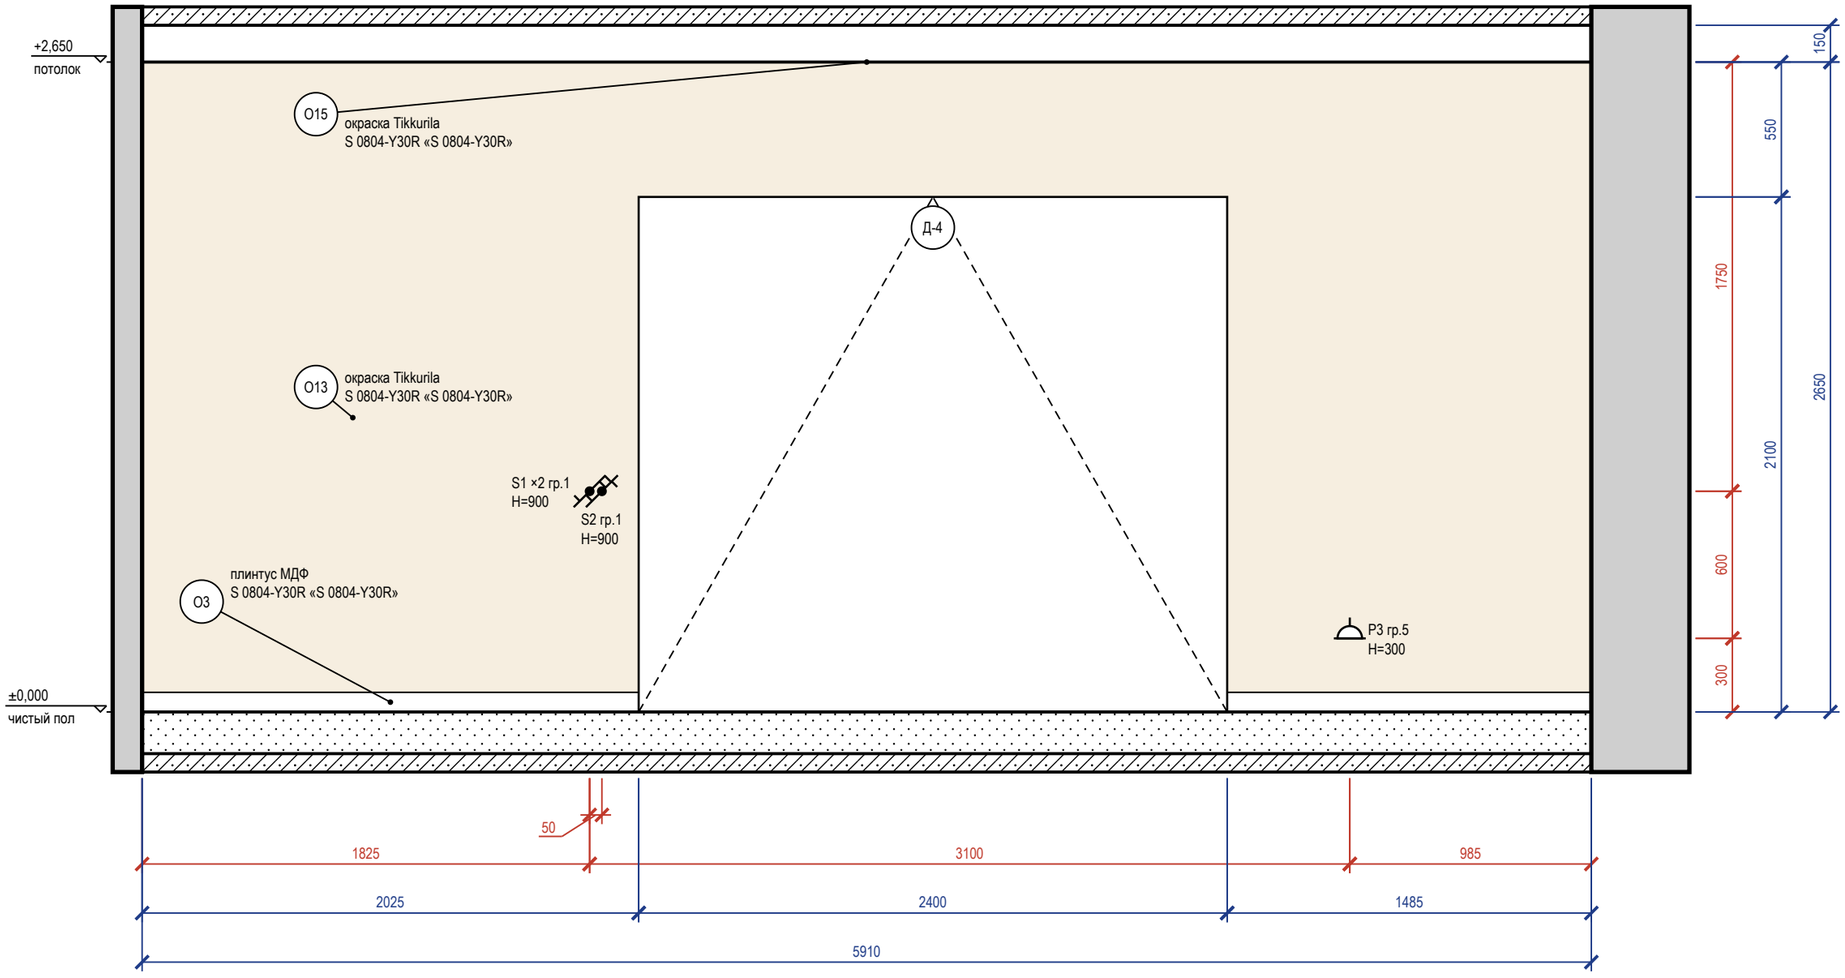


## Схема развёрток (М 1:100)

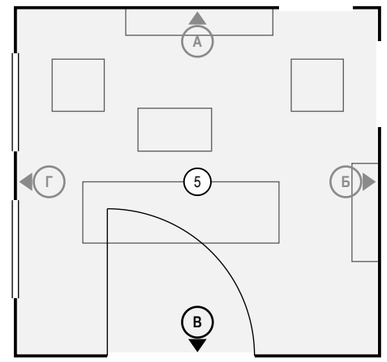


## Ведомость отделки (на листе)

| Марка | Поверхность | Материал, изделие | Цвет, код | Кол. |
|---|---|---|---|---|
| О3 | плинтус | плинтус МДФ, h 80 мм, аналог: плинтус МДФ под окраску 80×16 мм, полуглянцевая | NCS S 0804-Y30R «S 0804-Y30R» | 3,5 м |
| О13 | стены | окраска, Tikkurila Optiva 5 Matt, матовая, подготовка К3 | NCS S 0804-Y30R «S 0804-Y30R» | 10,6 м² |
| О15 | потолок | окраска, Tikkurila Anti-Reflex 2, глубокоматовая, подготовка Q3 | NCS S 0804-Y30R «S 0804-Y30R» | 33,7 м² |

Визуализация этой стены — лист 73

## Примечания

1. Размеры — в мм от чистовых поверхностей стен; условные обозначения и общие указания — лист 2.
2. Потолок на развёртках — по нижнему уровню У1; другие уровни потолка помещения: У2 +2,700.

| | | | | | |
|---|---|---|---|---|---|
| | | | | | Проект: Дом 331 м² |
| | Лист | № док. | Подпись | Дата | Развёртка стены В. Гостиная (пом. 5) |
| Дизайнер | Кырлан А.С. | | | 19.10.26 | |

| Стадия | Лист | Листов |
|---|---|---|
| П | 77 | 156 |

выпуск 18.10.2026 № 8cd922c868 · стр. 77 из 156

Правка к этому листу

## Развёртка стены Г

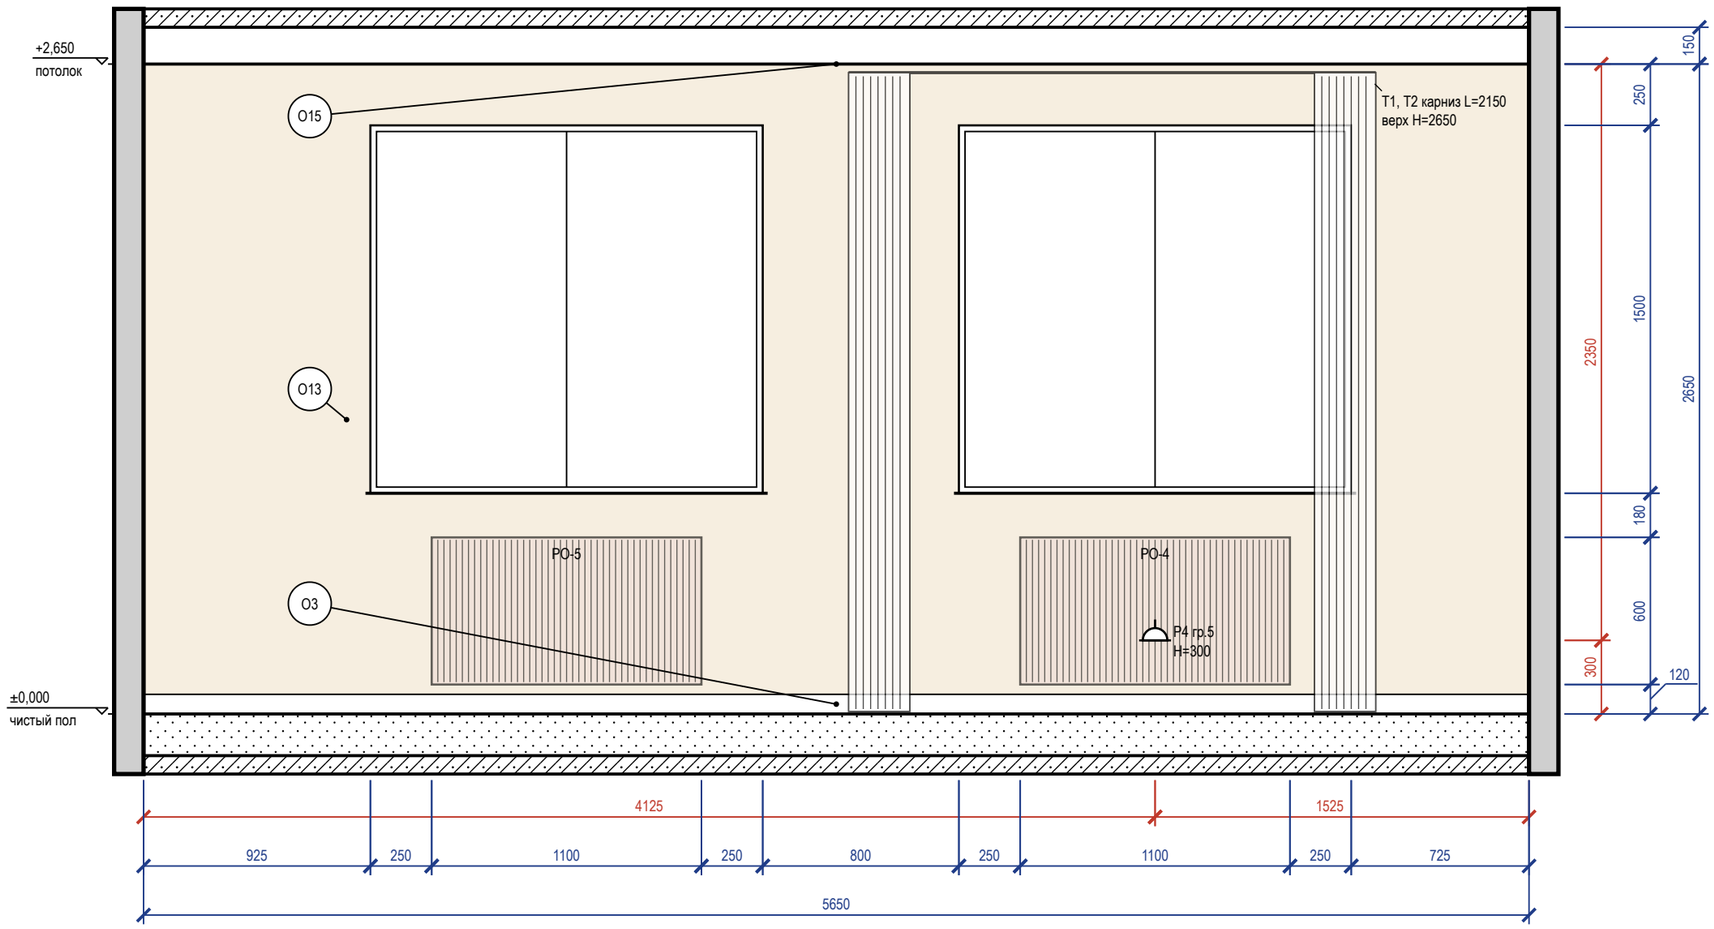


### Схема развёрток (М 1:100)

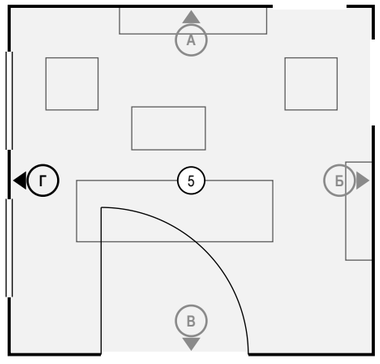


### Ведомость отделки (на листе)

| Марка | Поверхность | Материал, изделие | Цвет, код | Кол. |
|---|---|---|---|---|
| О3 | плинтус | плинтус МДФ, h 80 мм, аналог: плинтус МДФ под окраску 80×16 мм, полуглянцевая | NCS S 0804-Y30R «S 0804-Y30R» | 5,7 м |
| О13 | стены | окраска, Tikkurila Optiva 5 Matt, матовая, подготовка К3 | NCS S 0804-Y30R «S 0804-Y30R» | 10,2 м² |
| О15 | потолок | окраска, Tikkurila Anti-Reflex 2, глубокоматовая, подготовка Q3 | NCS S 0804-Y30R «S 0804-Y30R» | 33,7 м² |

Визуализация этой стены — лист 74

### Примечания

1. Размеры — в мм от чистовых поверхностей стен; условные обозначения и общие указания — лист 2.
2. Карнизы (шины) — по ведомости текстиля декоратора; длина L и верх Н — по развёртке, крепление — до окраски потолка.
3. Потолок на развёртках — по нижнему уровню У1; другие уровни потолка помещения: У2 +2,700.

| | Лист | № док. | Подпись | Дата |
|---|---|---|---|---|
| Дизайнер | Кырлан А.С. | | | 19.10.26 |

Проект: Дом 331 м²

Развёртка стены Г. Гостиная (пом. 5)

| Стадия | Лист | Листов |
|---|---|---|
| П | 78 | 156 |

Правка к этому листу

| | | | | | |
|---|---|---|---|---|---|
| | | | | | Проект: Дом 331 м² |
| | Лист | № док. | Подпись | Дата | |
| Дизайнер | Кырлан А.С. | | | 19.10.26 | Визуализация: Холл с лестницей |

| Стадия | Лист | Листов |
|---|---|---|
| П | 79 | 156 |

выпуск 18.10.2026 № 8cd922c868 · стр. 79 из 156

Правка к этому листу

## Развёртка стены А

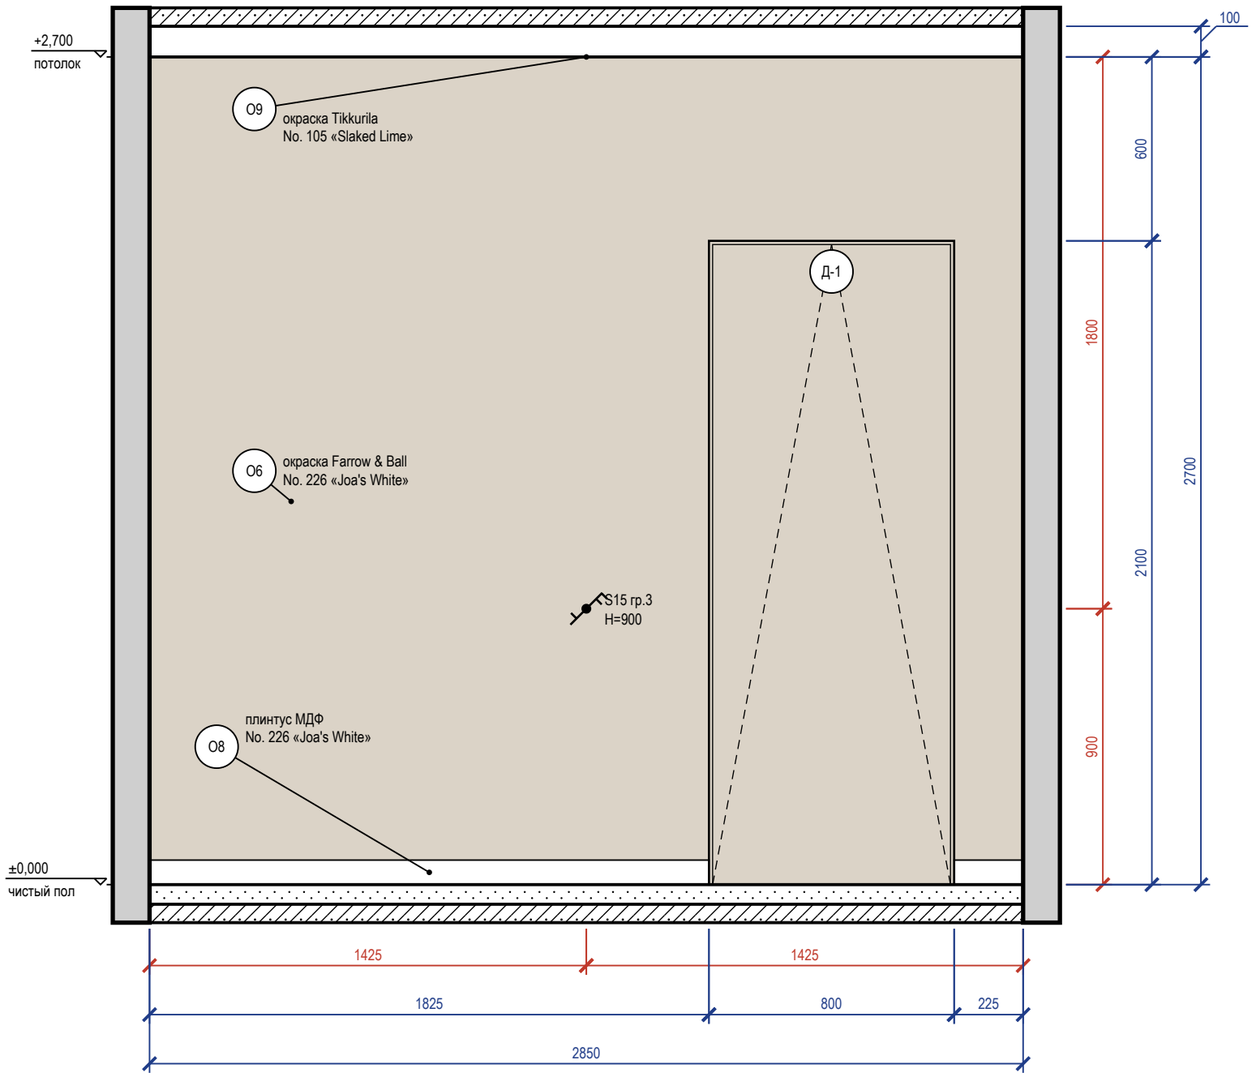


## Схема развёрток (М 1:100)

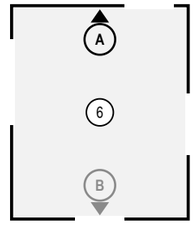


## Ведомость отделки (на листе)

| Марка | Поверхность | Материал, изделие | Цвет, код | Кол. |
|---|---|---|---|---|
| О6 | стены | окраска, Farrow & Ball Modern Emulsion, матовая, подготовка Q3 | Farrow & Ball No. 226 «Joa's White» | 6 м² |
| О8 | плинтус | плинтус МДФ, h 80 мм, аналог: плинтус МДФ под покраску 80×16 | Farrow & Ball No. 226 «Joa's White» | 2 м |
| О9 | потолок | окраска, Tikkurila Anti-Reflex 2, глубокоматовая, подготовка Q3 | Little Greene No. 105 «Slaked Lime» | 10 м² |

**3** **Дверь скрытого монтажа в плоскости стены, плинтус (М 1:10)**
Узел 3 — лист С3

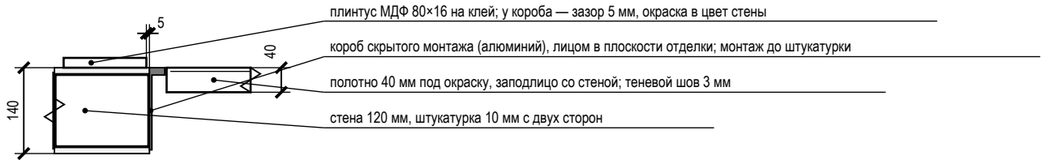


## Примечания

1. Размеры — в мм от чистовых поверхностей стен; условные обозначения и общие указания — лист 2.
2. Двери скрытого монтажа — полотно в плоскости стены, отделка стены по полотну, плинтус прерывается у короба (узел — на листе узлов).

| | | | | | |
|---|---|---|---|---|---|
| | | | | | Проект: Дом 331 м² |
| | Лист | № док. | Подпись | Дата | Развёртка стены А. Холл с лестницей (пом. 6) |
| Дизайнер | Кырлан А.С. | | | 19.10.26 | |

| Стадия | Лист | Листов |
|---|---|---|
| П | 80 | 156 |

выпуск 18.10.2026 № 8cd922c868 · стр. 80 из 156

Правка к этому листу

## Развёртка стены В

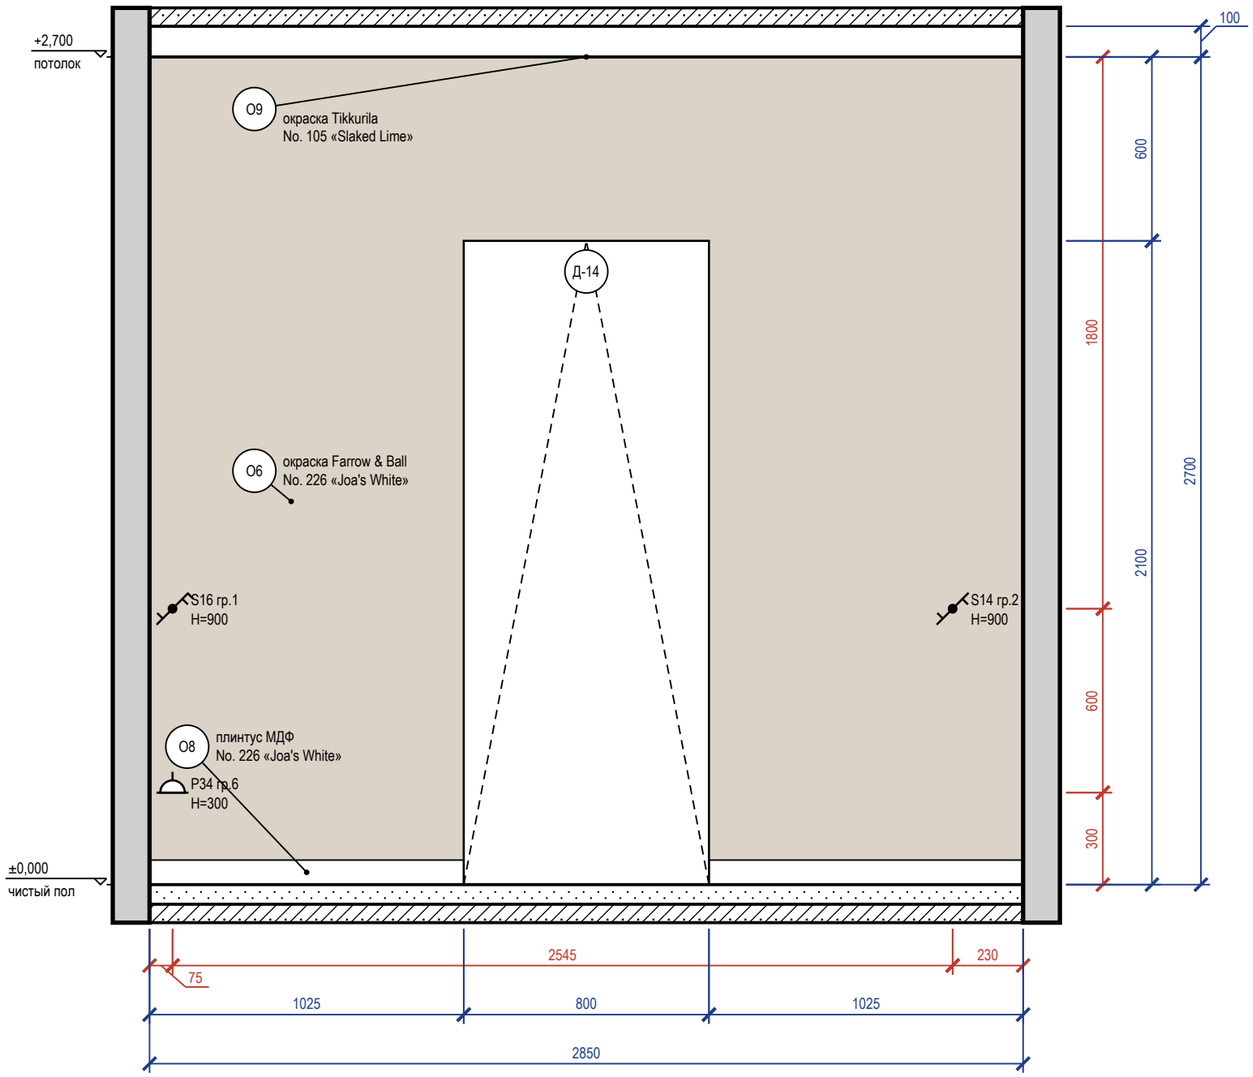


## Схема развёрток (М 1:100)

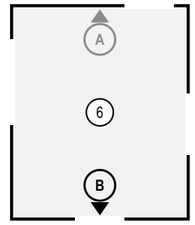


## Ведомость отделки (на листе)

| Марка | Поверхность | Материал, изделие | Цвет, код | Кол. |
|---|---|---|---|---|
| О6 | стены | окраска, Farrow & Ball Modern Emulsion, матовая, подготовка Q3 | Farrow & Ball No. 226 «Joa's White» | 6 м² |
| О8 | плинтус | плинтус МДФ, h 80 мм, аналог: плинтус МДФ под покраску 80×16 | Farrow & Ball No. 226 «Joa's White» | 2 м |
| О9 | потолок | окраска, Tikkurila Anti-Reflex 2, глубокоматовая, подготовка Q3 | Little Greene No. 105 «Slaked Lime» | 10 м² |

Визуализация этой стены — лист 79

## Примечания

1. Размеры — в мм от чистовых поверхностей стен; условные обозначения и общие указания — лист 2.

| | | | | | |
|---|---|---|---|---|---|
| | | | | | Проект: Дом 331 м² |
| | Лист | № док. | Подпись | Дата | |
| Дизайнер | Кырлан А.С. | | | 19.10.26 | Развёртка стены В. Холл с лестницей (пом. 6) |

| Стадия | Лист | Листов |
|---|---|---|
| П | 81 | 156 |

выпуск 18.10.2026 № 8cd922c868 · стр. 81 из 156

Правка к этому листу

| | | | | | |
|---|---|---|---|---|---|
| | | | | | Проект: Дом 331 м² |
| | | | | | |
| | Лист | № док. | Подпись | Дата | Визуализация кладовой |
| Дизайнер | Кырлан А.С. | | | 19.10.26 | |
| | | | | | |

| Стадия | Лист | Листов |
|---|---|---|
| П | 82 | 156 |

выпуск 18.10.2026 № 8cd922c868 · стр. 82 из 156

Правка к этому листу

## Развёртка стены В

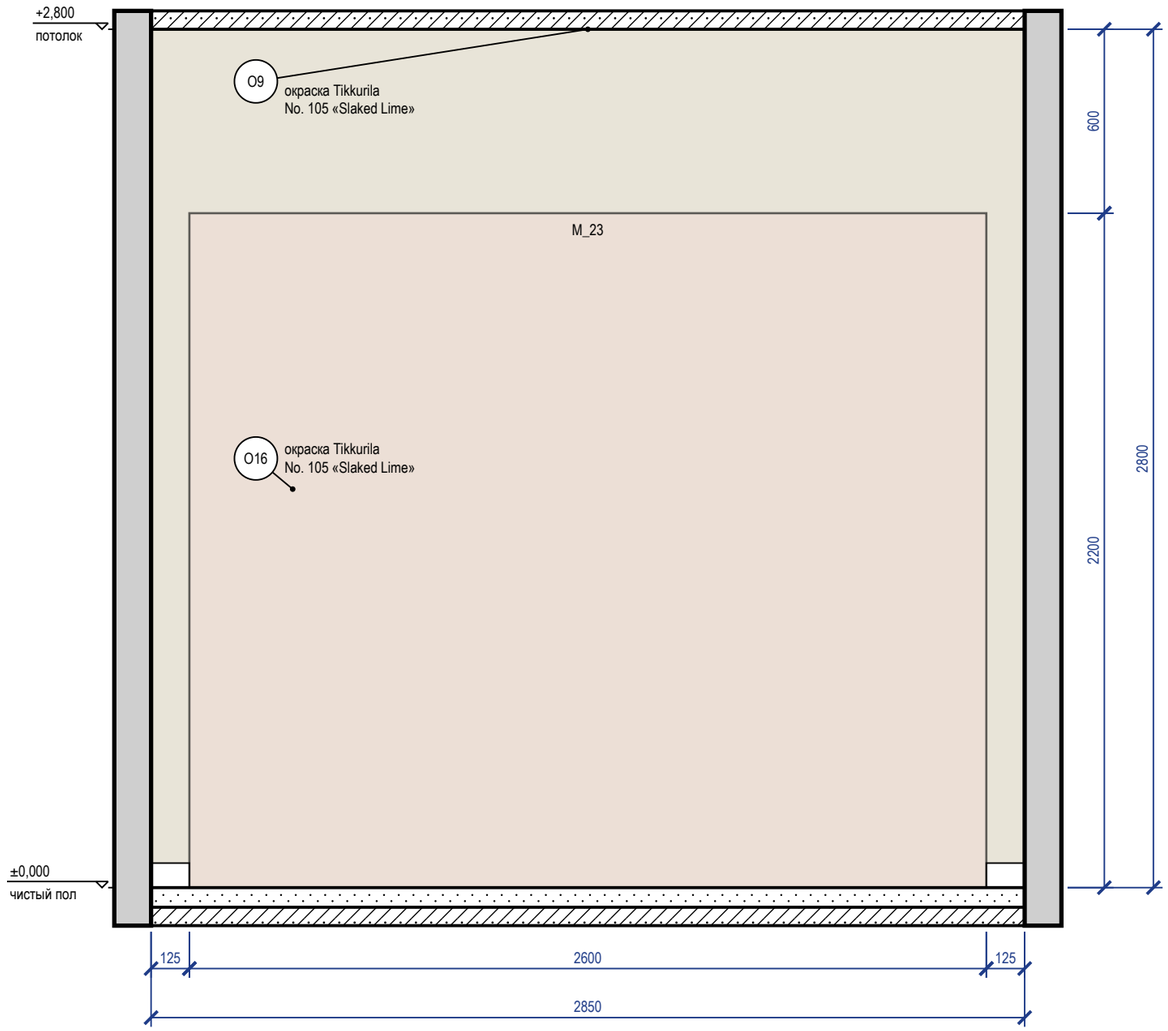


## Схема развёрток (М 1:100)

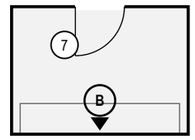


## Ведомость отделки (на листе)

| Марка | Поверхность | Материал, изделие | Цвет, код | Кол. |
|---|---|---|---|---|
| O9 | потолок | окраска, Tikkurila Anti-Reflex 2, глубокоматовая, подготовка Q3 | Little Greene No. 105 «Slaked Lime» | 6 м² |
| O16 | стены | окраска, Tikkurila Harmony, матовая, подготовка Q3 | Little Greene No. 105 «Slaked Lime» | 8 м² |
| O17 | плинтус | плинтус МДФ, h 80 мм, аналог: плинтус МДФ под покраску 80×16 | Little Greene No. 105 «Slaked Lime» | 0,3 м |

Визуализация этой стены — лист 82

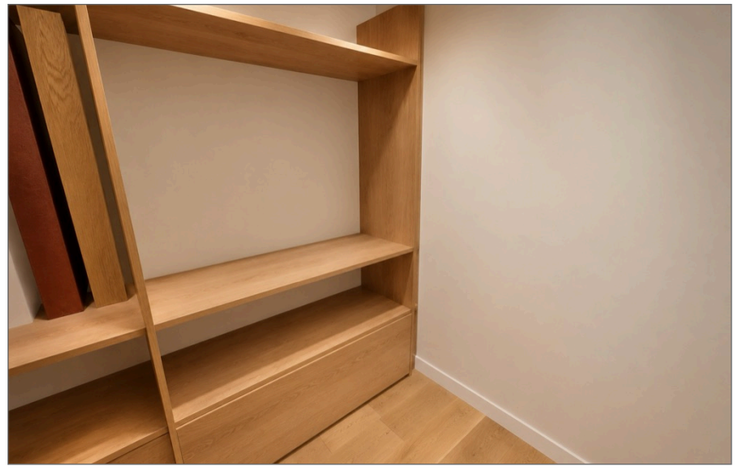

### Примечания

1. Размеры — в мм от чистовых поверхностей стен; условные обозначения и общие указания — лист 2.

| | | | | | |
|---|---|---|---|---|---|
| | | | | | Проект: Дом 331 м² |
| | Лист | № док. | Подпись | Дата | Развёртки стен. Кладовая (пом. 7) |
| Дизайнер | Кырлан А.С. | | | 19.10.26 | |

| Стадия | Лист | Листов |
|---|---|---|
| П | 83 | 156 |

выпуск 18.10.2026 № 8cd922c868 · стр. 83 из 156

Правка к этому листу

| | | | | | |
|---|---|---|---|---|---|
| | | | | | Проект: Дом 331 м² |
| | | | | | |
| | Лист | № док. | Подпись | Дата | Визуализация прихожей |
| Дизайнер | Кырлан А.С. | | | 19.10.26 | |

| Стадия | Лист | Листов |
|---|---|---|
| П | 84 | 156 |

выпуск 18.10.2026 № 8cd922c868 · стр. 84 из 156

Правка к этому листу

| | | | | | |
|---|---|---|---|---|---|
| | | | | | Проект: Дом 331 м² |
| | Лист | № док. | Подпись | Дата | |
| Дизайнер | Кырлан А.С. | | | 19.10.26 | Визуализация прихожей |

| Стадия | Лист | Листов |
|---|---|---|
| П | 85 | 156 |

выпуск 18.10.2026 № 8cd922c868 · стр. 85 из 156

## Развёртка стены А

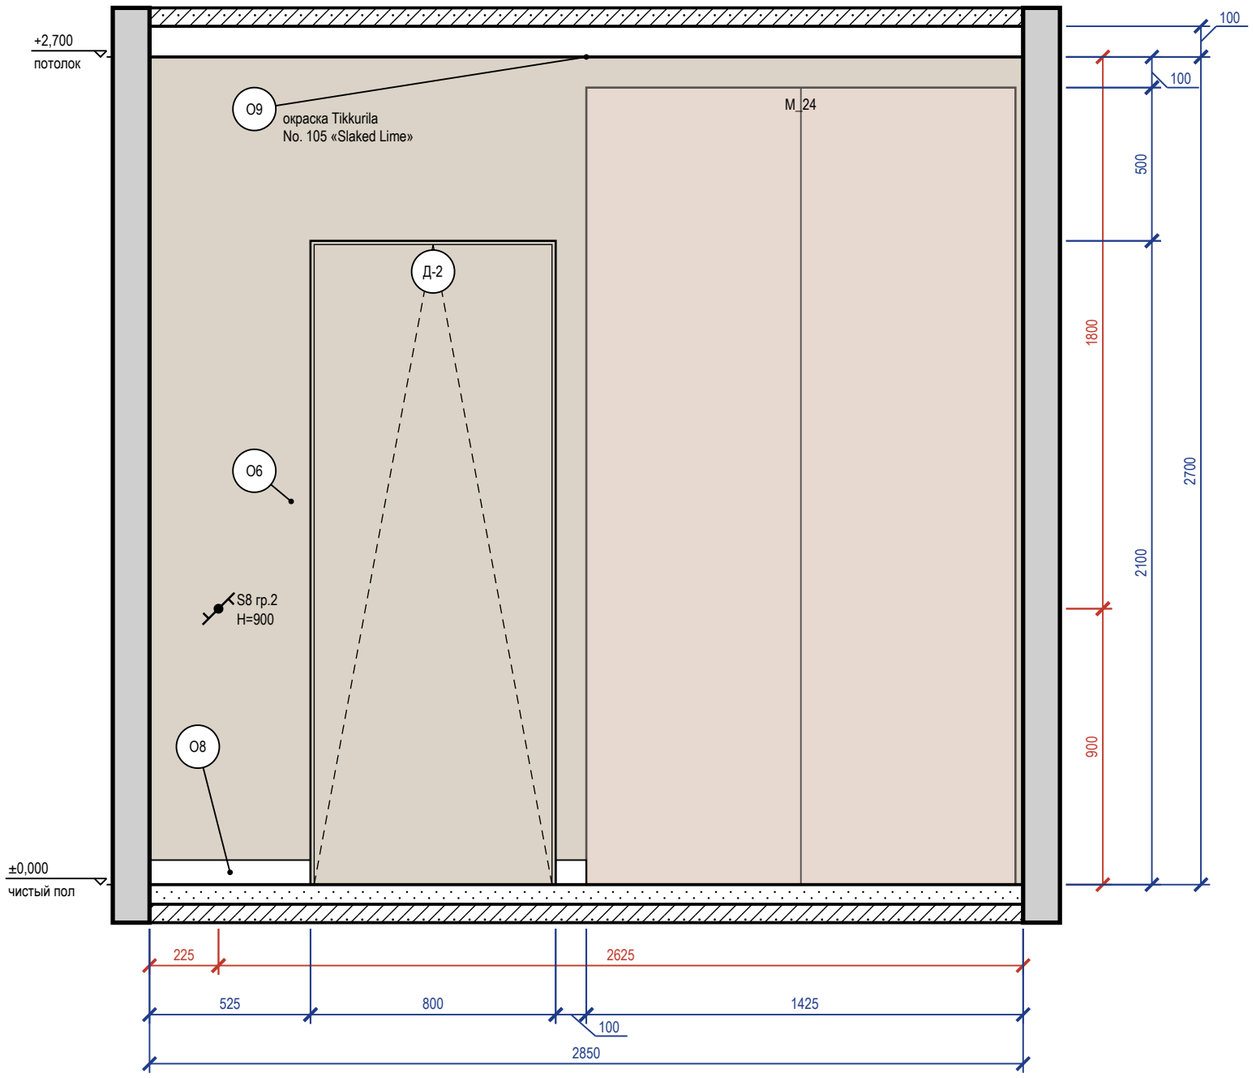


## Схема развёрток (М 1:100)

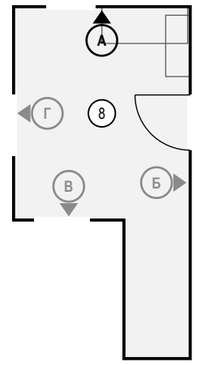


## Ведомость отделки (на листе)

| Марка | Поверхность | Материал, изделие | Цвет, код | Кол. |
|---|---|---|---|---|
| О6 | стены | окраска, Farrow & Ball Modern Emulsion, матовая, подготовка Q3 | Farrow & Ball No. 226 «Joa's White» | 6 м² |
| О8 | плинтус | плинтус МДФ, h 80 мм, аналог: плинтус МДФ под покраску 80×16 | Farrow & Ball No. 226 «Joa's White» | 0,6 м |
| О9 | потолок | окраска, Tikkurila Anti-Reflex 2, глубокоматовая, подготовка Q3 | Little Greene No. 105 «Slaked Lime» | 12,5 м² |

Визуализация этой стены — лист 84

### Примечания

1. Размеры — в мм от чистовых поверхностей стен; условные обозначения и общие указания — лист 2.
2. Двери скрытого монтажа — полотно в плоскости стены, отделка стены по полотну, плинтус прерывается у короба (узел — на листе узлов).

| | Лист | № док. | Подпись | Дата |
|---|---|---|---|---|
| Дизайнер | Кырлан А.С. | | | 19.10.26 |

Проект: Дом 331 м²

Развёртка стены А. Прихожая (пом. 8)

| Стадия | Лист | Листов |
|---|---|---|
| П | 86 | 156 |

Правка к этому листу

## Развёртка стены Б

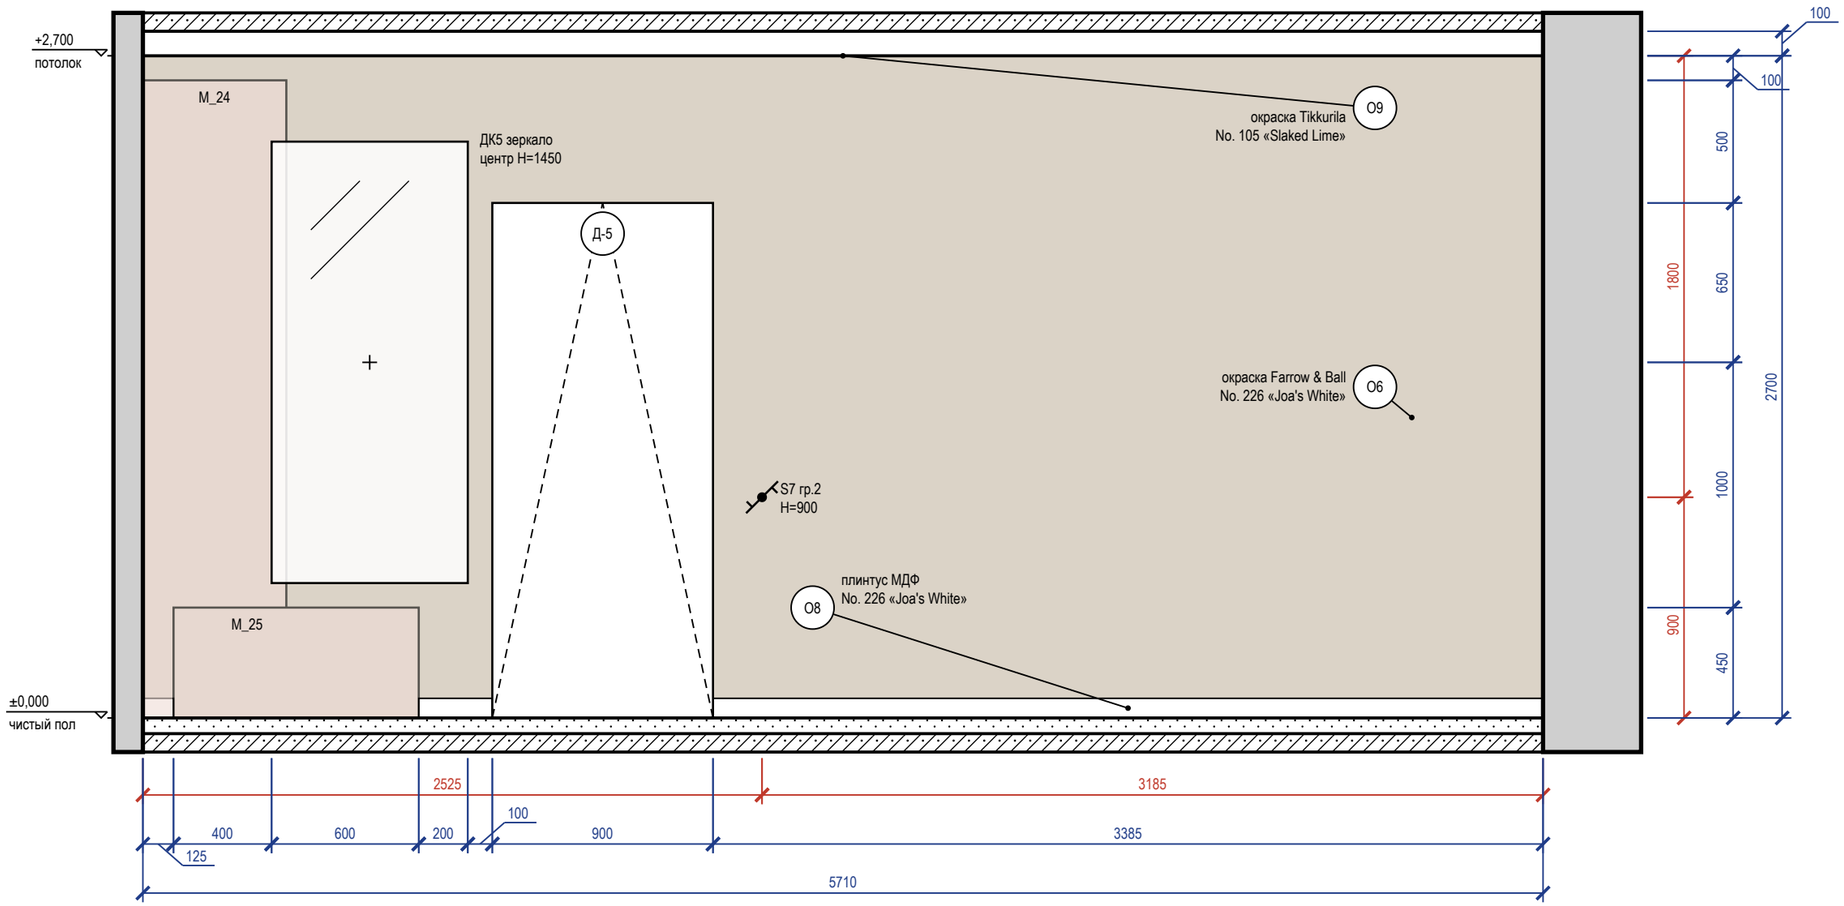


### Схема развёрток (М 1:100)

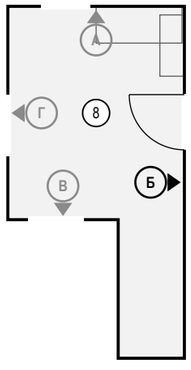


### Ведомость отделки (на листе)

| Марка | Поверхность | Материал, изделие | Цвет, код | Кол. |
|---|---|---|---|---|
| О6 | стены | окраска, Farrow & Ball Modern Emulsion, матовая, подготовка Q3 | Farrow & Ball No. 226 «Joa's White» | 13,5 м² |
| О8 | плинтус | плинтус МДФ, h 80 мм, аналог: плинтус МДФ под покраску 80×16 | Farrow & Ball No. 226 «Joa's White» | 3,8 м |
| О9 | потолок | окраска, Tikkurila Anti-Reflex 2, глубокоматовая, подготовка Q3 | Little Greene No. 105 «Slaked Lime» | 12,5 м² |

Визуализация этой стены — лист 85

### Примечания

1. Размеры — в мм от чистовых поверхностей стен; условные обозначения и общие указания — лист 2.
2. Картины и зеркала крепить к основанию по паспорту изделия (закладные и анкеры — в перечне скрытых работ); крест — ось центра предмета.

| | | | | | | | |
|---|---|---|---|---|---|---|---|
| | | | | | Проект: Дом 331 м² | | |
| | Лист | № док. | Подпись | Дата | Развёртка стены Б. Прихожая (пом. 8) | Стадия | Лист | Листов |
| Дизайнер | Кырлан А.С. | | | 19.10.26 | | П | 87 | 156 |

выпуск 18.10.2026 № 8cd922c868 · стр. 87 из 156

Правка к этому листу

## Развёртка стены В

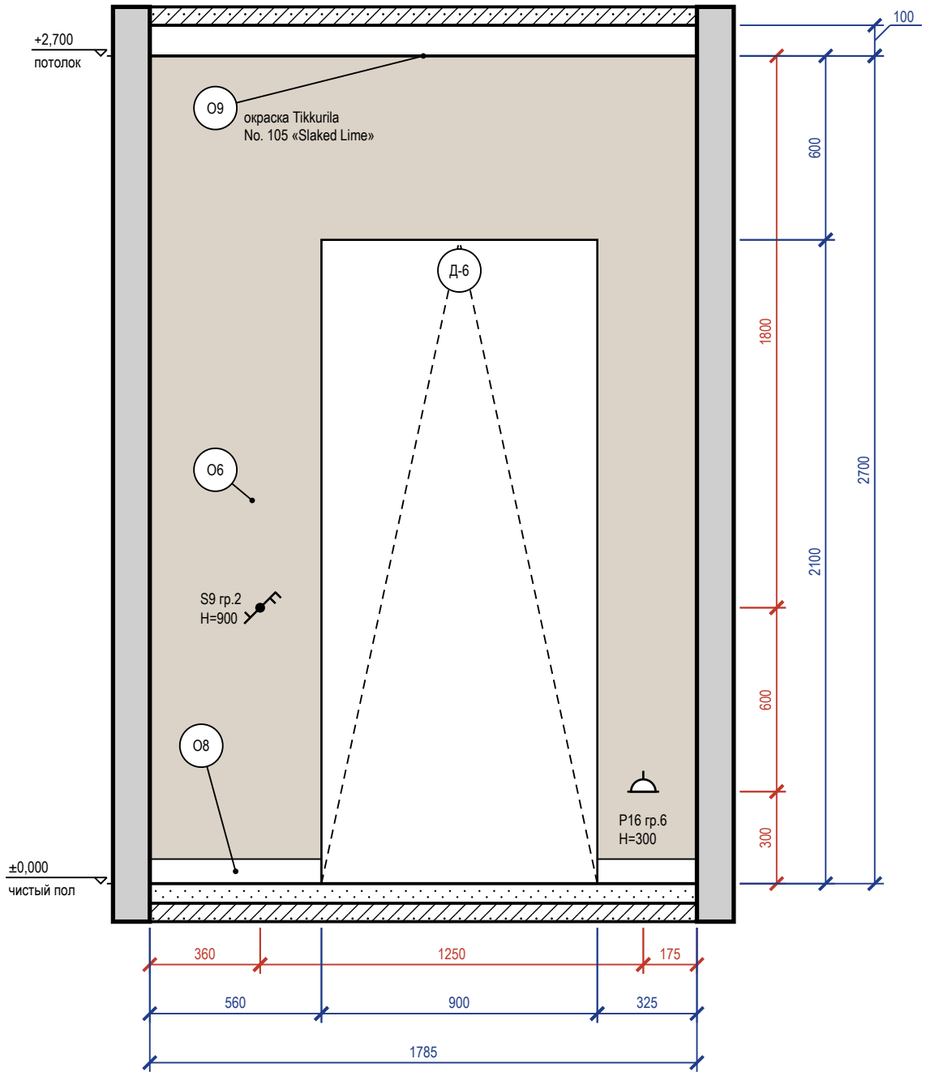


## Схема развёрток (М 1:100)

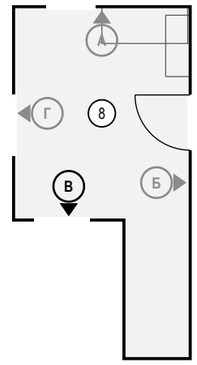


## Ведомость отделки (на листе)

| Марка | Поверхность | Материал, изделие | Цвет, код | Кол. |
|---|---|---|---|---|
| О6 | стены | окраска, Farrow & Ball Modern Emulsion, матовая, подготовка Q3 | Farrow & Ball No. 226 «Joa's White» | 2,9 м² |
| О8 | плинтус | плинтус МДФ, h 80 мм, аналог: плинтус МДФ под покраску 80×16 | Farrow & Ball No. 226 «Joa's White» | 0,9 м |
| О9 | потолок | окраска, Tikkurila Anti-Reflex 2, глубокоматовая, подготовка Q3 | Little Greene No. 105 «Slaked Lime» | 12,5 м² |

## Примечания

1. Размеры — в мм от чистовых поверхностей стен; условные обозначения и общие указания — лист 2.

| | | | | | |
|---|---|---|---|---|---|
| | | | | | Проект: Дом 331 м² |
| | Лист | № док. | Подпись | Дата | Развёртка стены В. Прихожая (пом. 8) |
| Дизайнер | Кырлан А.С. | | | 19.10.26 | |

| Стадия | Лист | Листов |
|---|---|---|
| П | 88 | 156 |

выпуск 18.10.2026 № 8cd922c868 · стр. 88 из 156

Правка к этому листу

## Развёртка стены Г

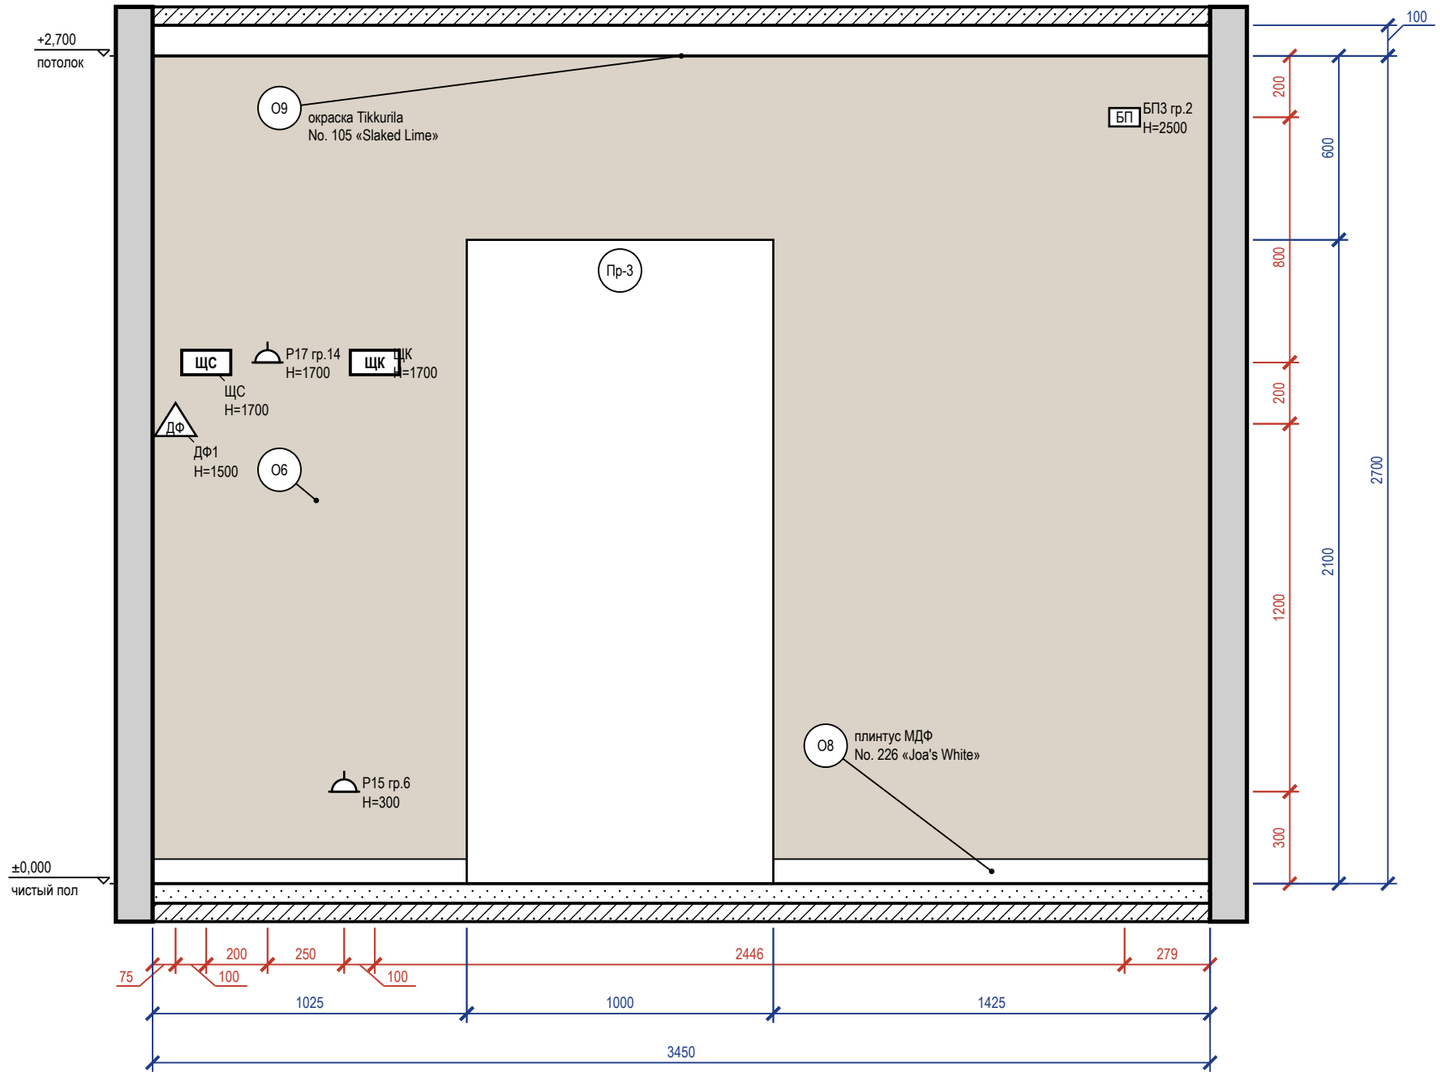


## Схема развёрток (М 1:100)

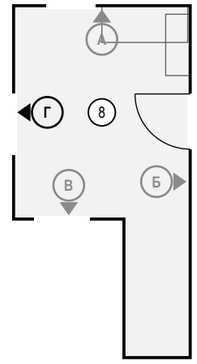


## Ведомость отделки (на листе)

| Марка | Поверхность | Материал, изделие | Цвет, код | Кол. |
|---|---|---|---|---|
| О6 | стены | окраска, Farrow & Ball Modern Emulsion, матовая, подготовка Q3 | Farrow & Ball No. 226 «Joa's White» | 7,2 м² |
| О8 | плинтус | плинтус МДФ, h 80 мм, аналог: плинтус МДФ под покраску 80×16 | Farrow & Ball No. 226 «Joa's White» | 2,5 м |
| О9 | потолок | окраска, Tikkurila Anti-Reflex 2, глубокоматовая, подготовка Q3 | Little Greene No. 105 «Slaked Lime» | 12,5 м² |

## Примечания

1. Размеры — в мм от чистовых поверхностей стен; условные обозначения и общие указания — лист 2.

| | | | | | |
|---|---|---|---|---|---|
| | | | | | Проект: Дом 331 м² |
| | Лист | № док. | Подпись | Дата | Развёртка стены Г. Прихожая (пом. 8) |
| Дизайнер | Кырлан А.С. | | | 19.10.26 | |

| Стадия | Лист | Листов |
|---|---|---|
| П | 89 | 156 |

Правка к этому листу

## Развёртка стены Г

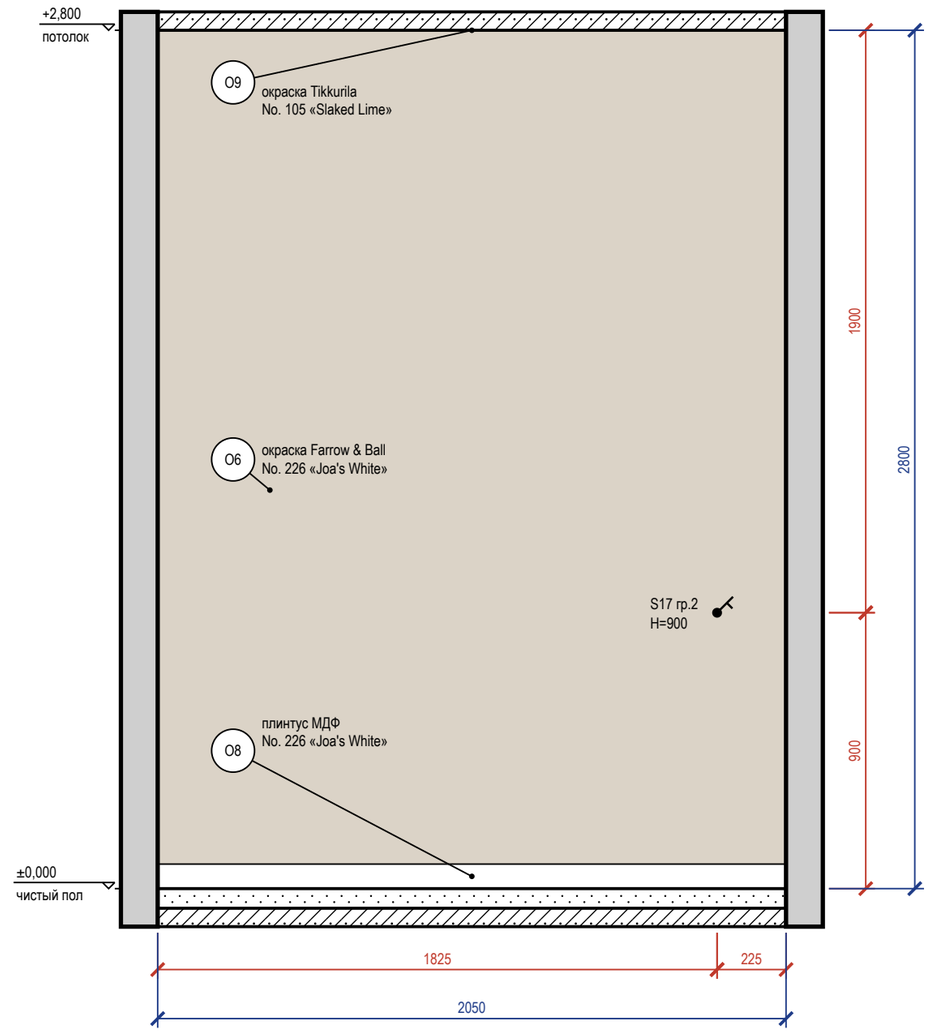


## Схема развёрток (М 1:100)

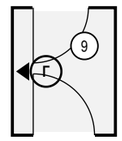


## Ведомость отделки (на листе)

| Марка | Поверхность | Материал, изделие | Цвет, код | Кол. |
|---|---|---|---|---|
| О6 | стены | окраска, Farrow & Ball Modern Emulsion, матовая, подготовка Q3 | Farrow & Ball No. 226 «Joa's White» | 5,7 м² |
| О8 | плинтус | плинтус МДФ, h 80 мм, аналог: плинтус МДФ под покраску 80×16 | Farrow & Ball No. 226 «Joa's White» | 2 м |
| О9 | потолок | окраска, Tikkurila Anti-Reflex 2, глубокоматовая, подготовка Q3 | Little Greene No. 105 «Slaked Lime» | 3,5 м² |

## Примечания

1. Размеры — в мм от чистовых поверхностей стен; условные обозначения и общие указания — лист 2.

| | | | | | |
|---|---|---|---|---|---|
| | | | | | Проект: Дом 331 м² |
| | Лист | № док. | Подпись | Дата | Развёртки стен. Тамбур (пом. 9) |
| Дизайнер | Кырлан А.С. | | | 19.10.26 | |

| Стадия | Лист | Листов |
|---|---|---|
| П | 90 | 156 |

выпуск 18.10.2026 № 8cd922c868 · стр. 90 из 156

Правка к этому листу

| | | | | | | |
|---|---|---|---|---|---|---|
| | | | | | Проект: Дом 331 м² | |
| | Лист | № док. | Подпись | Дата | Визуализация: Гараж | Стадия / Лист / Листов |
| Дизайнер | Кырлан А.С. | | | 19.10.26 | | П / 91 / 156 |

выпуск 18.10.2026 № 8cd922c868 · стр. 91 из 156

Правка к этому листу

## Развёртка стены А

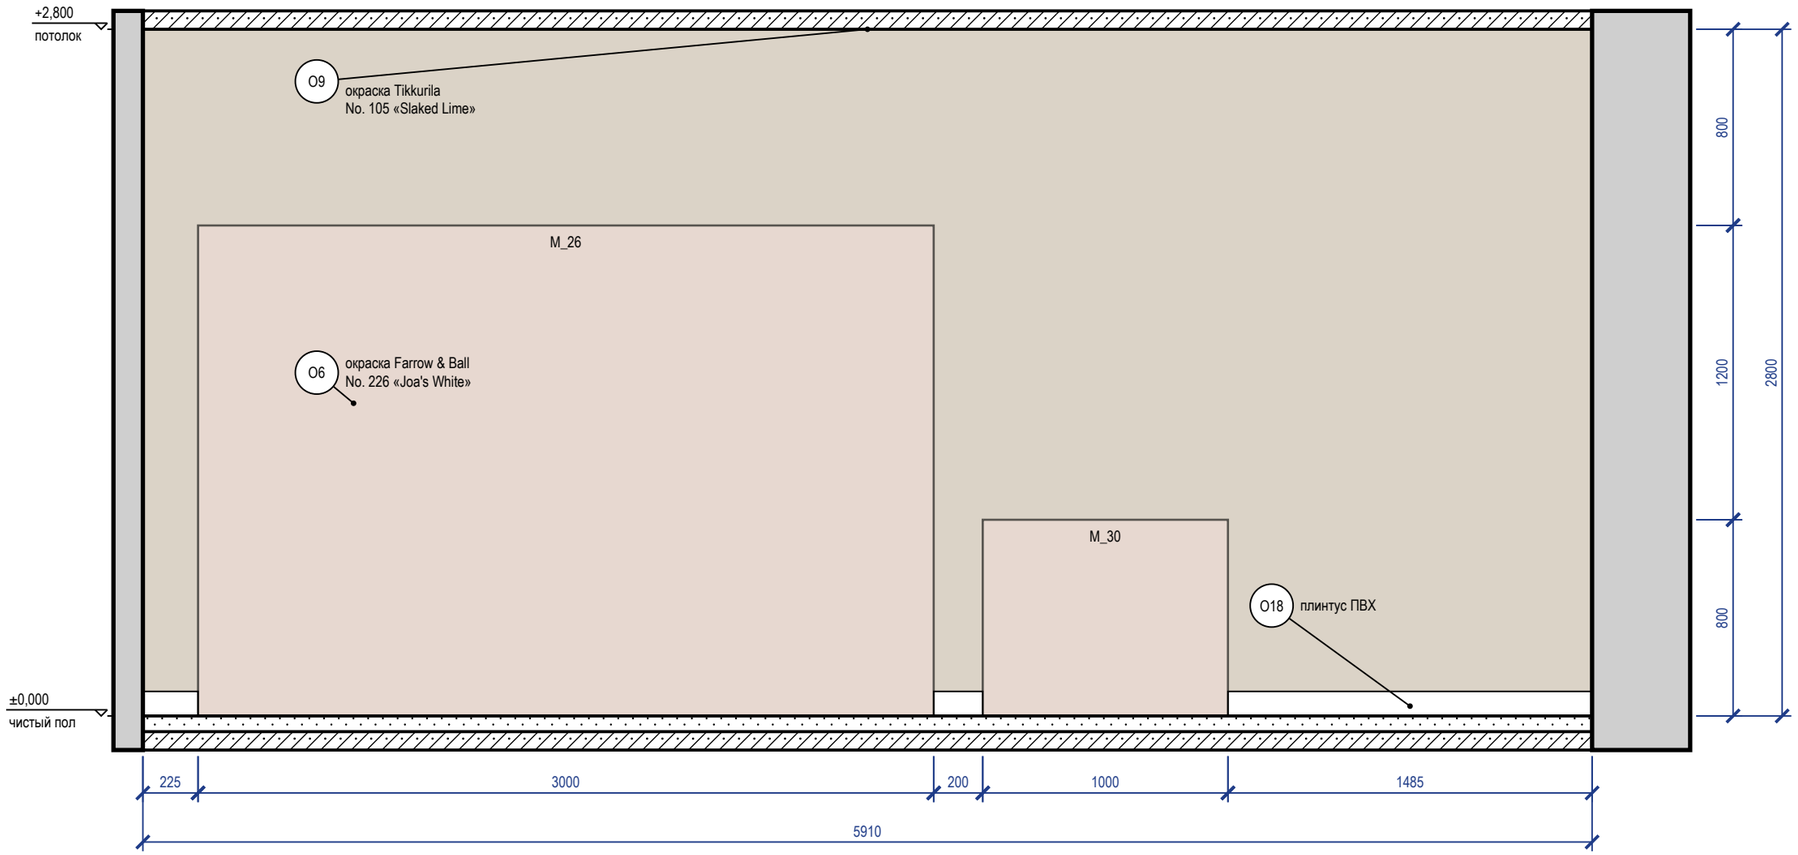


### Схема развёрток (М 1:100)

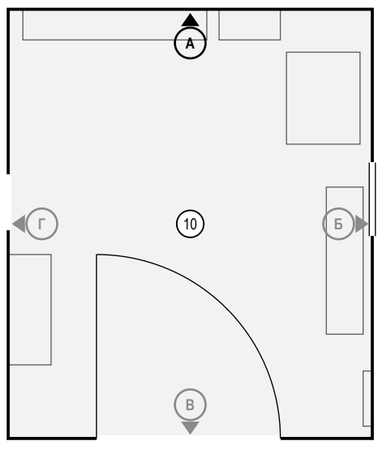


### Ведомость отделки (на листе)

| Марка | Поверхность | Материал, изделие | Цвет, код | Кол. |
|---|---|---|---|---|
| О6 | стены | окраска, Farrow & Ball Modern Emulsion, матовая, подготовка Q3 | Farrow & Ball No. 226 «Joa's White» | 16,5 м² |
| О9 | потолок | окраска, Tikkurila Anti-Reflex 2, глубокоматовая, подготовка Q3 | Little Greene No. 105 «Slaked Lime» | 41,6 м² |
| О18 | плинтус | плинтус ПВХ, h 100 мм, аналог: плинтус ПВХ влагостойкий 100 мм, серый | | 1,9 м |

Визуализация этой стены — лист 91

### Примечания

1. Размеры — в мм от чистовых поверхностей стен; условные обозначения и общие указания — лист 2.

| | | | | | |
|---|---|---|---|---|---|
| | | | | | Проект: Дом 331 м² |
| | Лист | № док. | Подпись | Дата | Развёртка стены А. Гараж (пом. 10) |
| Дизайнер | Кырлан А.С. | | | 19.10.26 | |

| Стадия | Лист | Листов |
|---|---|---|
| П | 92 | 156 |

выпуск 18.10.2026 № 8cd922c868 · стр. 92 из 156

Правка к этому листу

## Развёртка стены Б

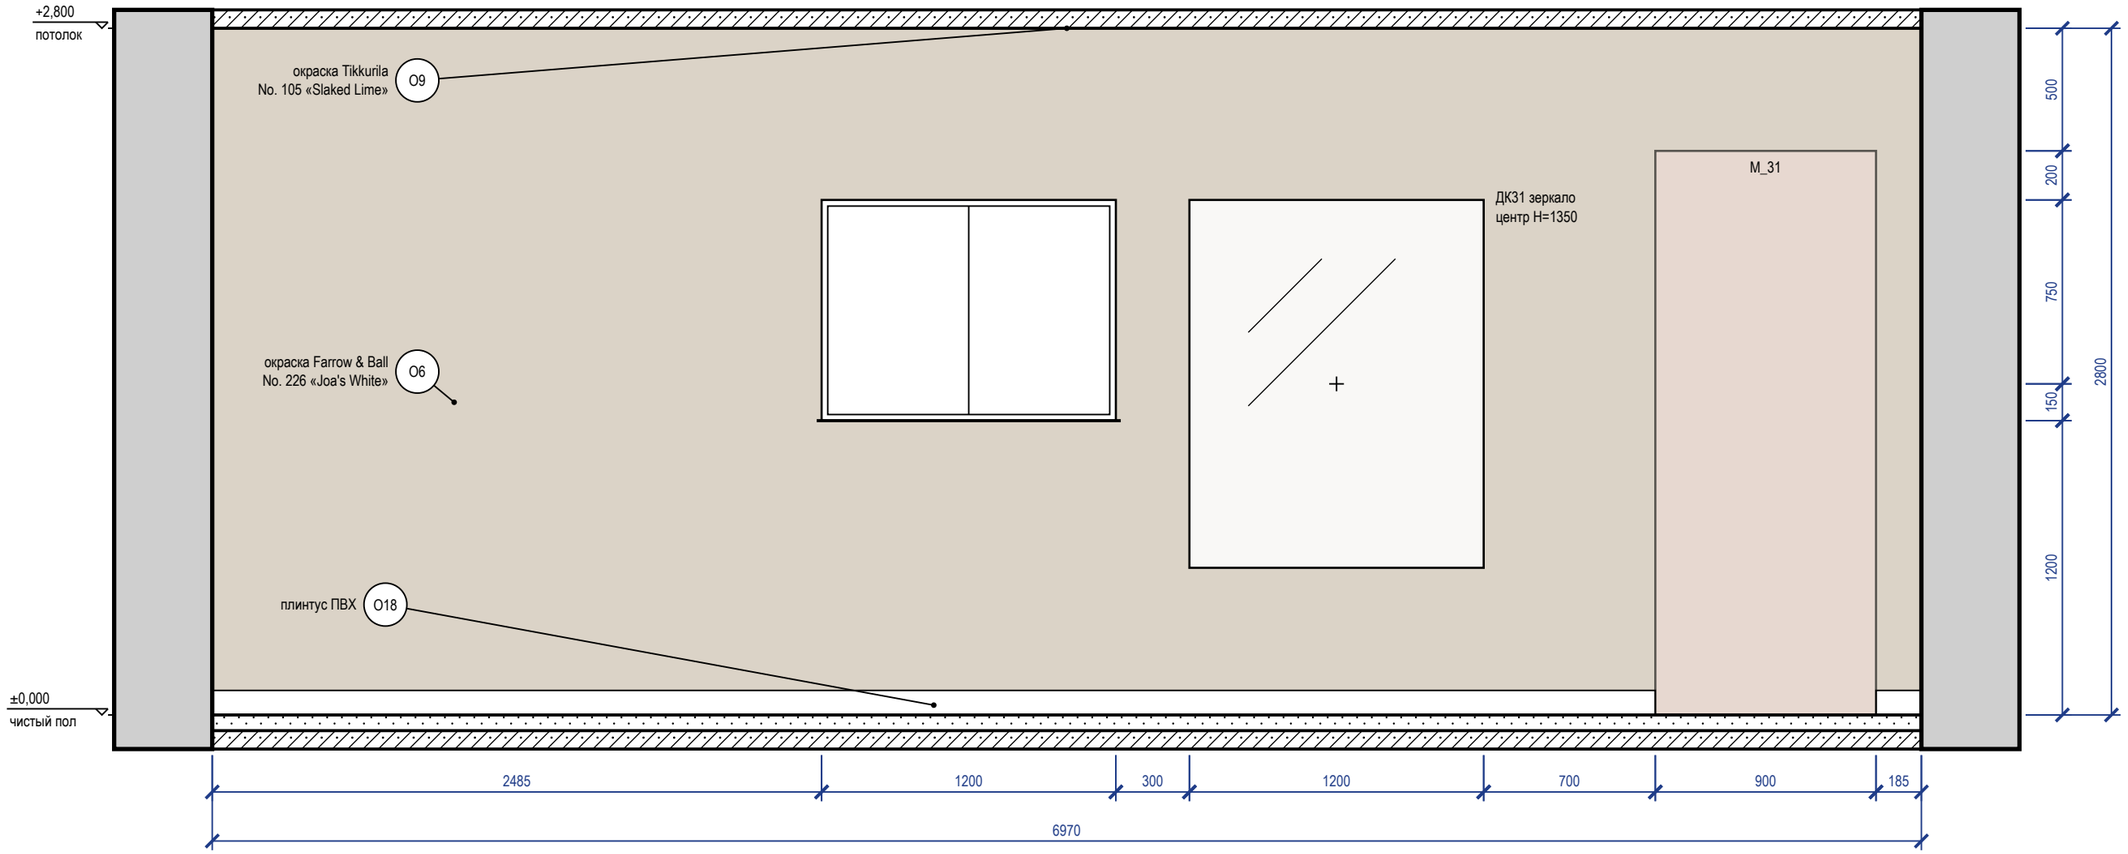


### Схема развёрток (М 1:100)

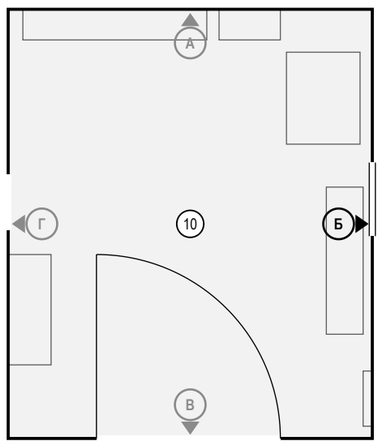


### Ведомость отделки (на листе)

| Марка | Поверхность | Материал, изделие | Цвет, код | Кол. |
|---|---|---|---|---|
| О6 | стены | окраска, Farrow & Ball Modern Emulsion, матовая, подготовка Q3 | Farrow & Ball No. 226 «Joa's White» | 18,4 м² |
| О9 | потолок | окраска, Tikkurila Anti-Reflex 2, глубокоматовая, подготовка Q3 | Little Greene No. 105 «Slaked Lime» | 41,6 м² |
| О18 | плинтус | плинтус ПВХ, h 100 мм, аналог: плинтус ПВХ влагостойкий 100 мм, серый | | 6,1 м |

### Примечания

1. Размеры — в мм от чистовых поверхностей стен; условные обозначения и общие указания — лист 2.
2. Картины и зеркала крепить к основанию по паспорту изделия (закладные и анкеры — в перечне скрытых работ); крест — ось центра предмета.

| | | | | | |
|---|---|---|---|---|---|
| | | | | | Проект: Дом 331 м² |
| | Лист | № док. | Подпись | Дата | |
| Дизайнер | Кырлан А.С. | | | 19.10.26 | Развёртка стены Б. Гараж (пом. 10) |

| Стадия | Лист | Листов |
|---|---|---|
| П | 93 | 156 |

выпуск 18.10.2026 № 8cd922c868 · стр. 93 из 156

Правка к этому листу

## Развёртка стены В

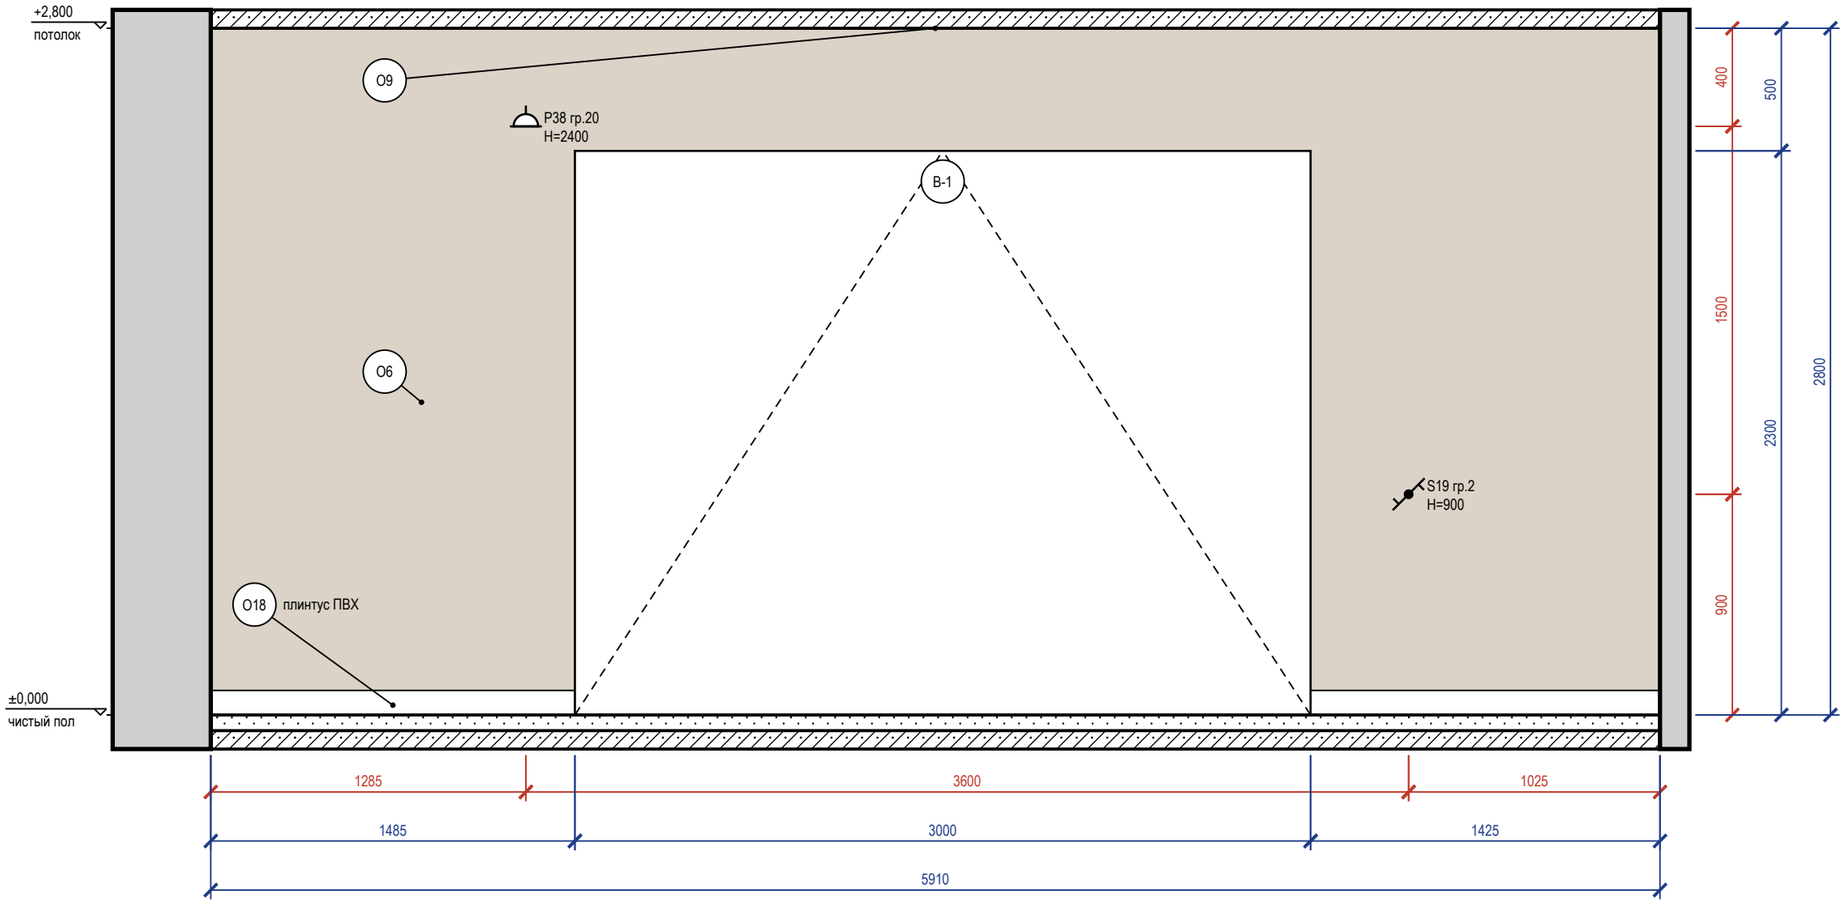


## Схема развёрток (М 1:100)

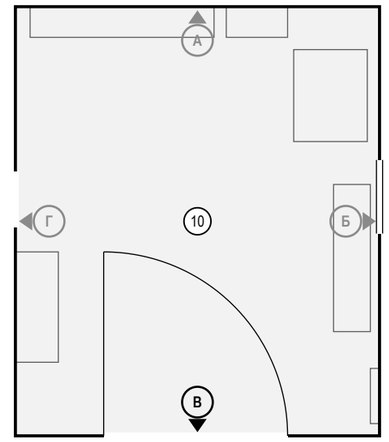


## Ведомость отделки (на листе)

| Марка | Поверхность | Материал, изделие | Цвет, код | Кол. |
|---|---|---|---|---|
| О6 | стены | окраска, Farrow & Ball Modern Emulsion, матовая, подготовка Q3 | Farrow & Ball No. 226 «Joa's White» | 9,6 м² |
| О9 | потолок | окраска, Tikkurila Anti-Reflex 2, глубокоматовая, подготовка Q3 | Little Greene No. 105 «Slaked Lime» | 41,6 м² |
| О18 | плинтус | плинтус ПВХ, h 100 мм, аналог: плинтус ПВХ влагостойкий 100 мм, серый | | 2,9 м |

## Примечания

1. Размеры — в мм от чистовых поверхностей стен; условные обозначения и общие указания — лист 2.

| | | | | | |
|---|---|---|---|---|---|
| | | | | | Проект: Дом 331 м² |
| | Лист | № док. | Подпись | Дата | Развёртка стены В. Гараж (пом. 10) |
| Дизайнер | Кырлан А.С. | | | 19.10.26 | |

| Стадия | Лист | Листов |
|---|---|---|
| П | 94 | 156 |

выпуск 18.10.2026 № 8cd922c868 · стр. 94 из 156

Правка к этому листу

## Развёртка стены Г

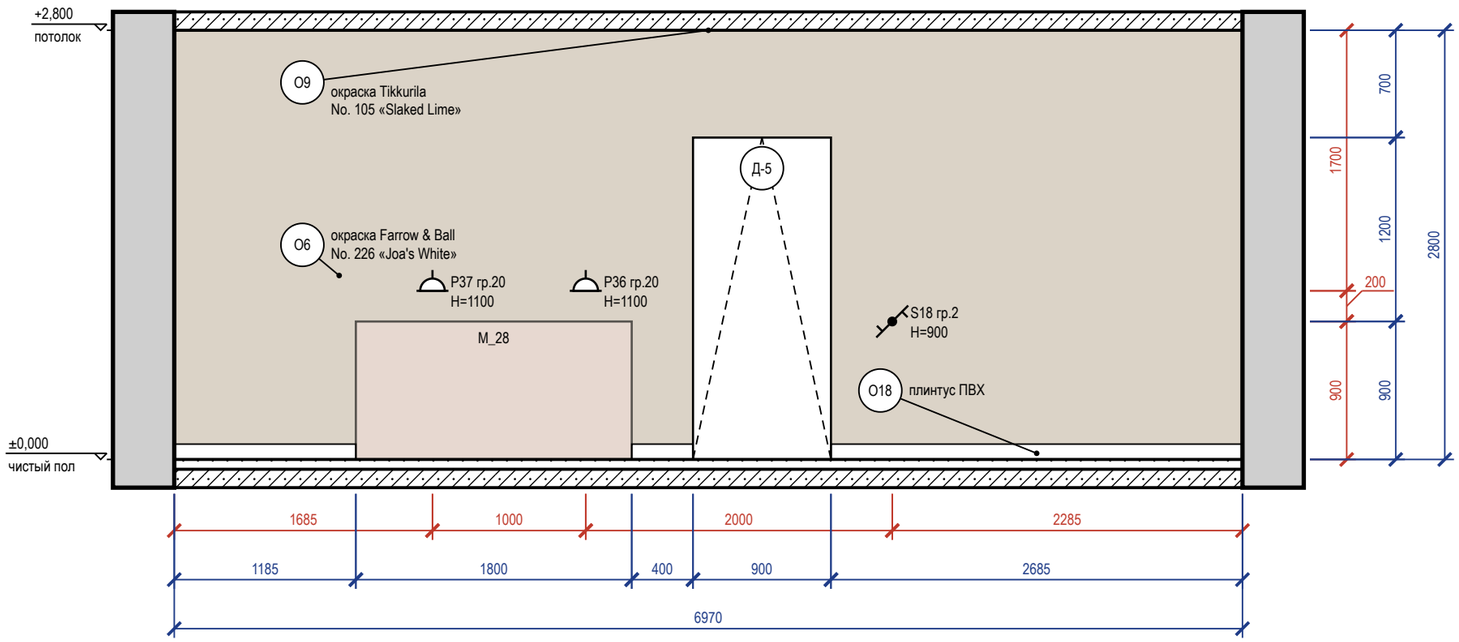


## Схема развёрток (М 1:100)

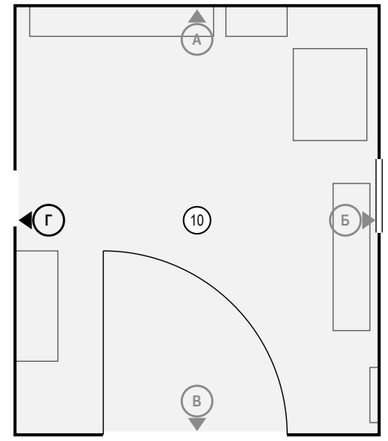


## Ведомость отделки (на листе)

| Марка | Поверхность | Материал, изделие | Цвет, код | Кол. |
|---|---|---|---|---|
| О6 | стены | окраска, Farrow & Ball Modern Emulsion, матовая, подготовка Q3 | Farrow & Ball No. 226 «Joa's White» | 17,6 м² |
| О9 | потолок | окраска, Tikkurila Anti-Reflex 2, глубокоматовая, подготовка Q3 | Little Greene No. 105 «Slaked Lime» | 41,6 м² |
| О18 | плинтус | плинтус ПВХ, h 100 мм, аналог: плинтус ПВХ влагостойкий 100 мм, серый | | 4,3 м |

### Примечания

1. Размеры — в мм от чистовых поверхностей стен; условные обозначения и общие указания — лист 2.

| | Лист | № док. | Подпись | Дата |
|---|---|---|---|---|
| Дизайнер | Кырлан А.С. | | | 19.10.26 |

Проект: Дом 331 м²

Развёртка стены Г. Гараж (пом. 10)

| Стадия | Лист | Листов |
|---|---|---|
| П | 95 | 156 |

выпуск 18.10.2026 № 8cd922c868 · стр. 95 из 156

Правка к этому листу

| | | | | | |
|---|---|---|---|---|---|
| | | | | | Проект: Дом 331 м² |
| | Лист | № док. | Подпись | Дата | |
| Дизайнер | Кырлан А.С. | | | 19.10.26 | Визуализация: Веранда |

| Стадия | Лист | Листов |
|---|---|---|
| П | 96 | 156 |

выпуск 18.10.2026 № 8cd922c868 · стр. 96 из 156

Правка к этому листу

## Развёртка стены А

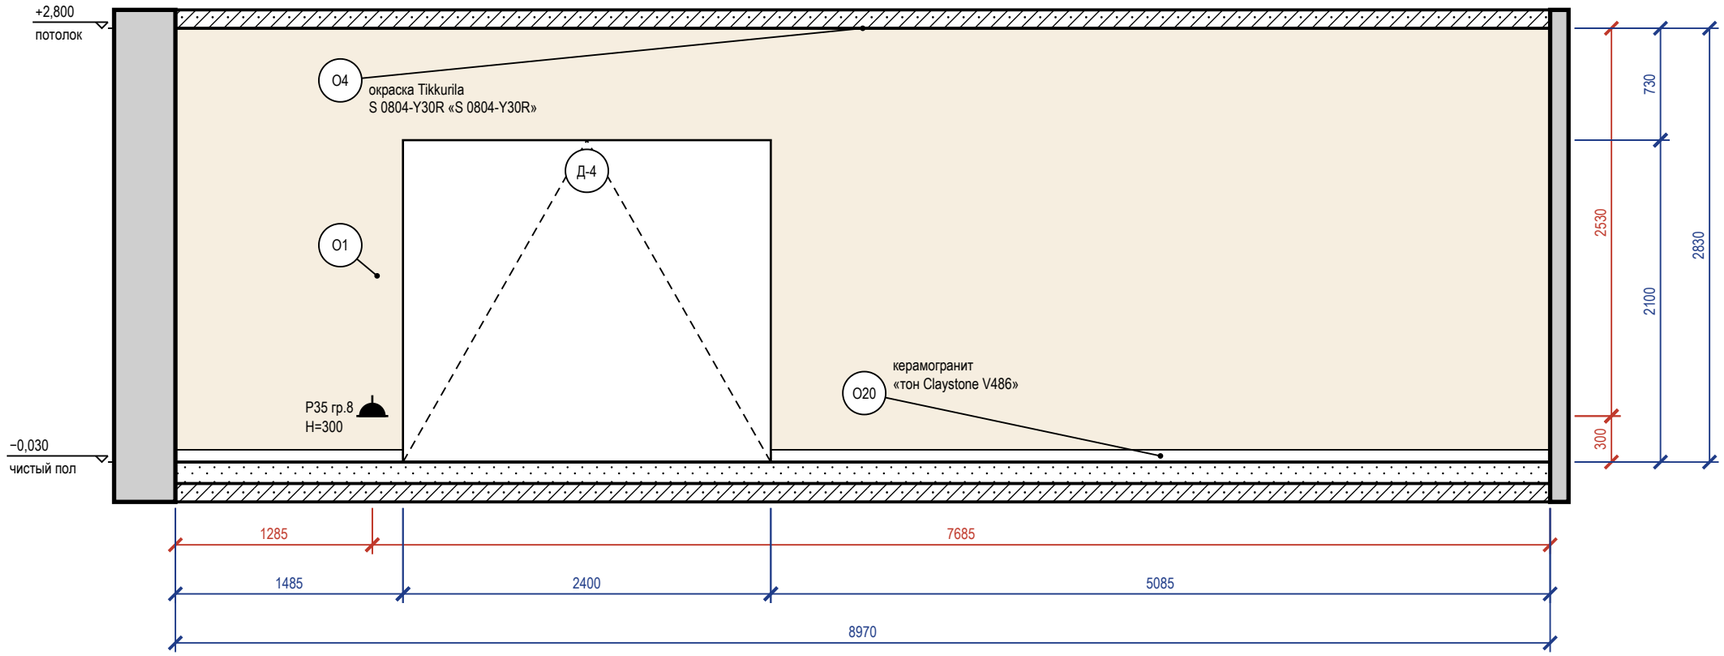


### Схема развёрток (М 1:100)

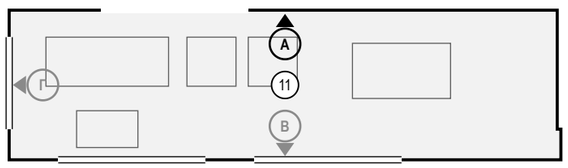


### Ведомость отделки (на листе)

| Марка | Поверхность | Материал, изделие | Цвет, код | Кол. |
|---|---|---|---|---|
| О1 | стены | окраска, Tikkurila Luja 7, шелковисто-матовая, подготовка К3 | NCS S 0804-Y30R «S 0804-Y30R» | 20,3 м² |
| О4 | потолок | окраска, Tikkurila Luja 7, матовая, подготовка Q3 | NCS S 0804-Y30R «S 0804-Y30R» | 21,8 м² |
| О20 | плинтус | керамогранит, аналог: плинтус из керамогранита пола, подрезка 80 мм, верхняя кромка с запилом 45° | #B8AFA5 «тон Claystone V486» | 6,6 м |

### Примечания

1. Размеры — в мм от чистовых поверхностей стен; условные обозначения и общие указания — лист 2.

| | | | | | |
|---|---|---|---|---|---|
| | | | | | Проект: Дом 331 м² |
| | Лист | № док. | Подпись | Дата | Развёртка стены А. Веранда (пом. 11) |
| Дизайнер | Кырлан А.С. | | | 19.10.26 | |

| Стадия | Лист | Листов |
|---|---|---|
| П | 97 | 156 |

выпуск 18.10.2026 № 8cd922c868 · стр. 97 из 156

Правка к этому листу

## Развёртка стены В

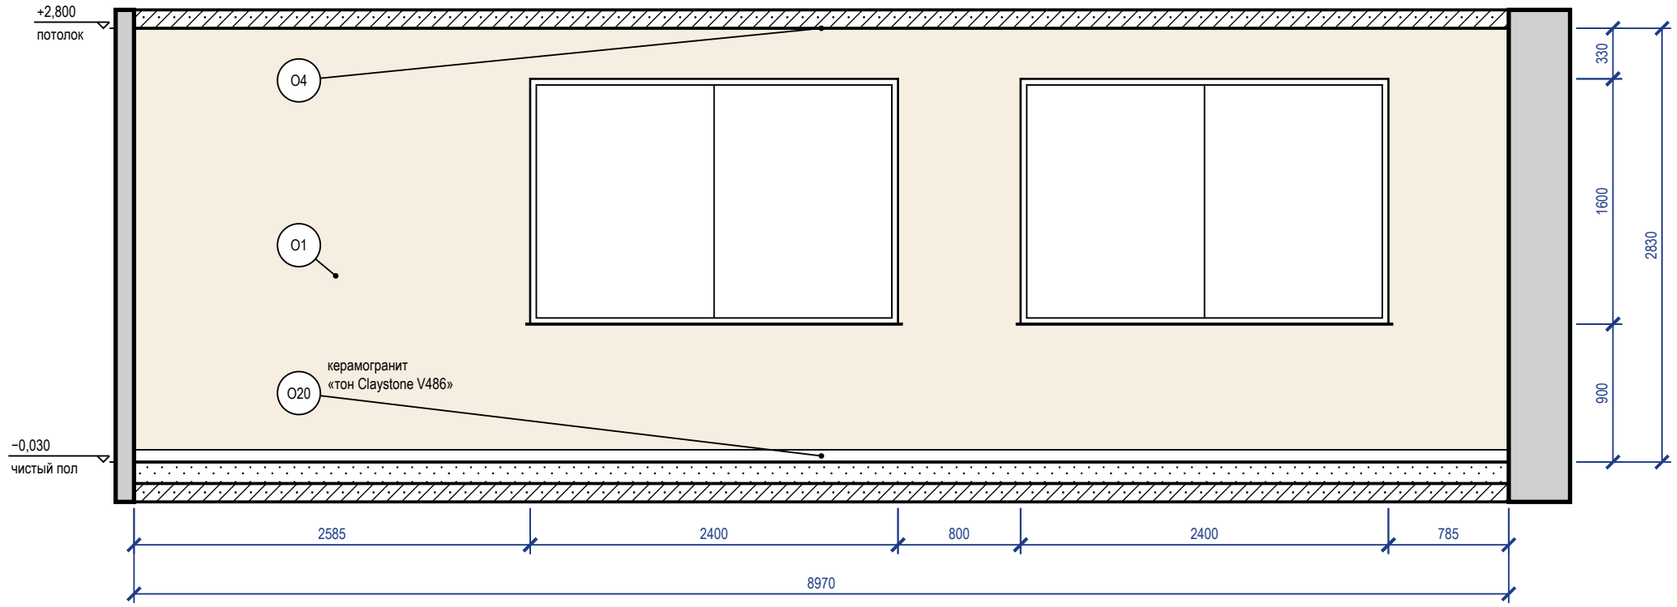


### Схема развёрток (М 1:100)

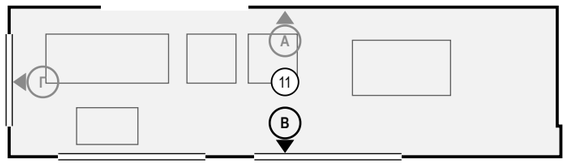


### Ведомость отделки (на листе)

| Марка | Поверхность | Материал, изделие | Цвет, код | Кол. |
|---|---|---|---|---|
| О1 | стены | окраска, Tikkurila Luja 7, шелковисто-матовая, подготовка К3 | NCS S 0804-Y30R «S 0804-Y30R» | 17,7 м² |
| О4 | потолок | окраска, Tikkurila Luja 7, матовая, подготовка Q3 | NCS S 0804-Y30R «S 0804-Y30R» | 21,8 м² |
| О20 | плинтус | керамогранит, аналог: плинтус из керамогранита пола, подрезка 80 мм, верхняя кромка с запилом 45° | #B8AFA5 «тон Claystone V486» | 9 м |

Визуализация этой стены — лист 96

### Примечания

1. Размеры — в мм от чистовых поверхностей стен; условные обозначения и общие указания — лист 2.

| | | | | | |
|---|---|---|---|---|---|
| | | | | | Проект: Дом 331 м² |
| | Лист | № док. | Подпись | Дата | |
| Дизайнер | Кырлан А.С. | | | 19.10.26 | Развёртка стены В. Веранда (пом. 11) |

| Стадия | Лист | Листов |
|---|---|---|
| П | 98 | 156 |

выпуск 18.10.2026 № 8cd922c868 · стр. 98 из 156

Правка к этому листу

## Развёртка стены Г

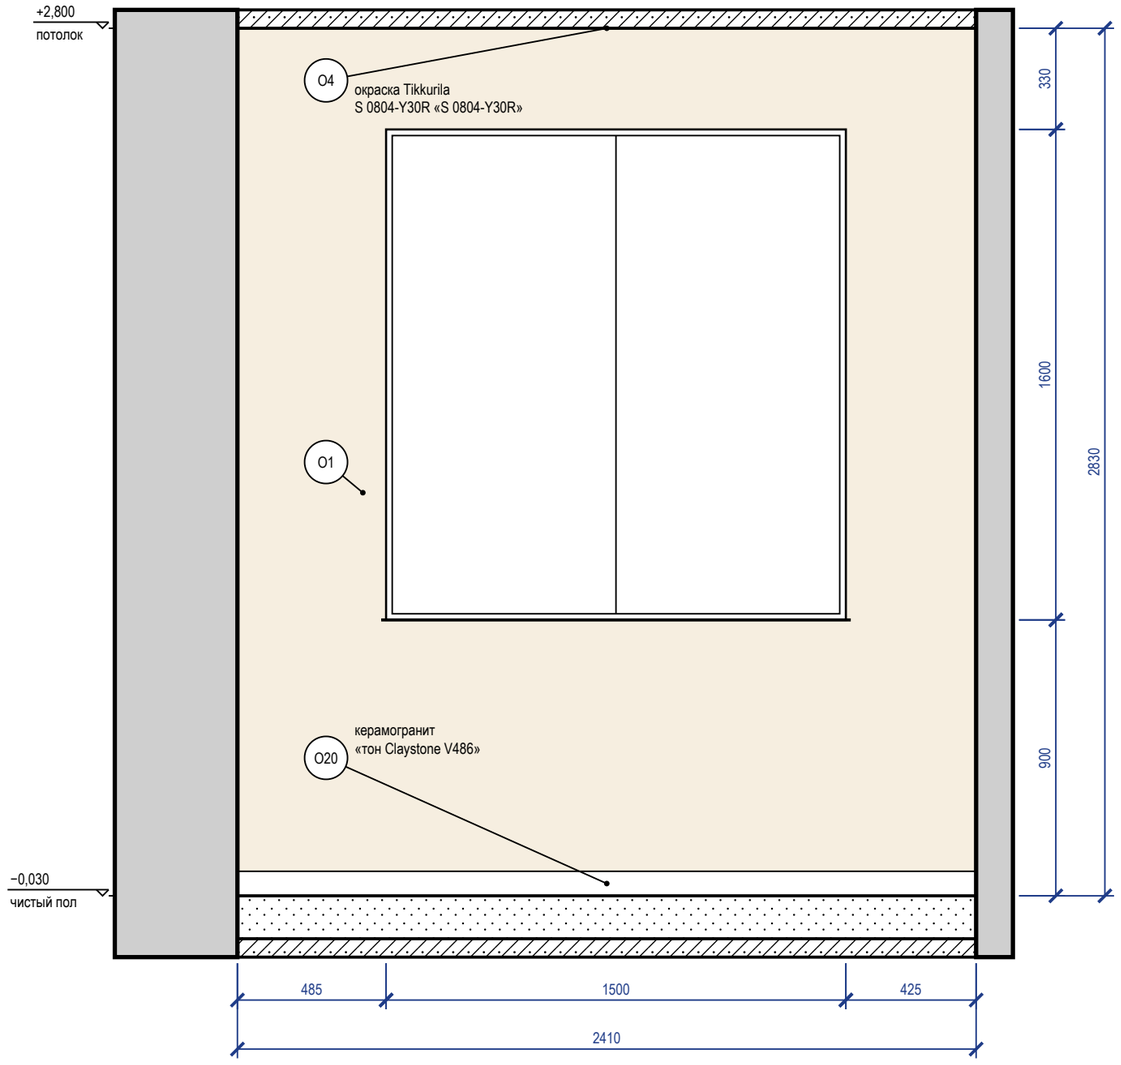


## Схема развёрток (М 1:100)

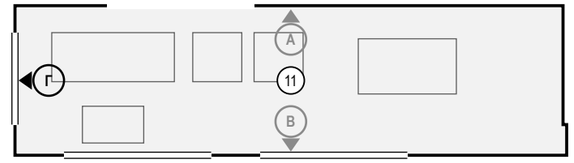


## Ведомость отделки (на листе)

| Марка | Поверхность | Материал, изделие | Цвет, код | Кол. |
|---|---|---|---|---|
| О1 | стены | окраска, Tikkurila Luja 7, шелковисто-матовая, подготовка К3 | NCS S 0804-Y30R «S 0804-Y30R» | 4,4 м² |
| О4 | потолок | окраска, Tikkurila Luja 7, матовая, подготовка Q3 | NCS S 0804-Y30R «S 0804-Y30R» | 21,8 м² |
| О20 | плинтус | керамогранит, аналог: плинтус из керамогранита пола, подрезка 80 мм, верхняя кромка с запилом 45° | #B8AFA5 «тон Claystone V486» | 2,4 м |

## Примечания

1. Размеры — в мм от чистовых поверхностей стен; условные обозначения и общие указания — лист 2.

| | | | | | |
|---|---|---|---|---|---|
| | Лист | № док. | Подпись | Дата | |
| Дизайнер | Кырлан А.С. | | | 19.10.26 | Развёртка стены Г. Веранда (пом. 11) |

Проект: Дом 331 м²

| Стадия | Лист | Листов |
|---|---|---|
| П | 99 | 156 |

выпуск 18.10.2026 № 8cd922c868 · стр. 99 из 156

Правка к этому листу

| | | | | | |
|---|---|---|---|---|---|
| | | | | | Проект: Дом 331 м² |
| | Лист | № док. | Подпись | Дата | Визуализация: Крыльцо |
| Дизайнер | Кырлан А.С. | | | 19.10.26 | |

| Стадия | Лист | Листов |
|---|---|---|
| П | 100 | 156 |

выпуск 18.10.2026 № 8cd922c868 · стр. 100 из 156

Правка к этому листу

## Развёртка стены А

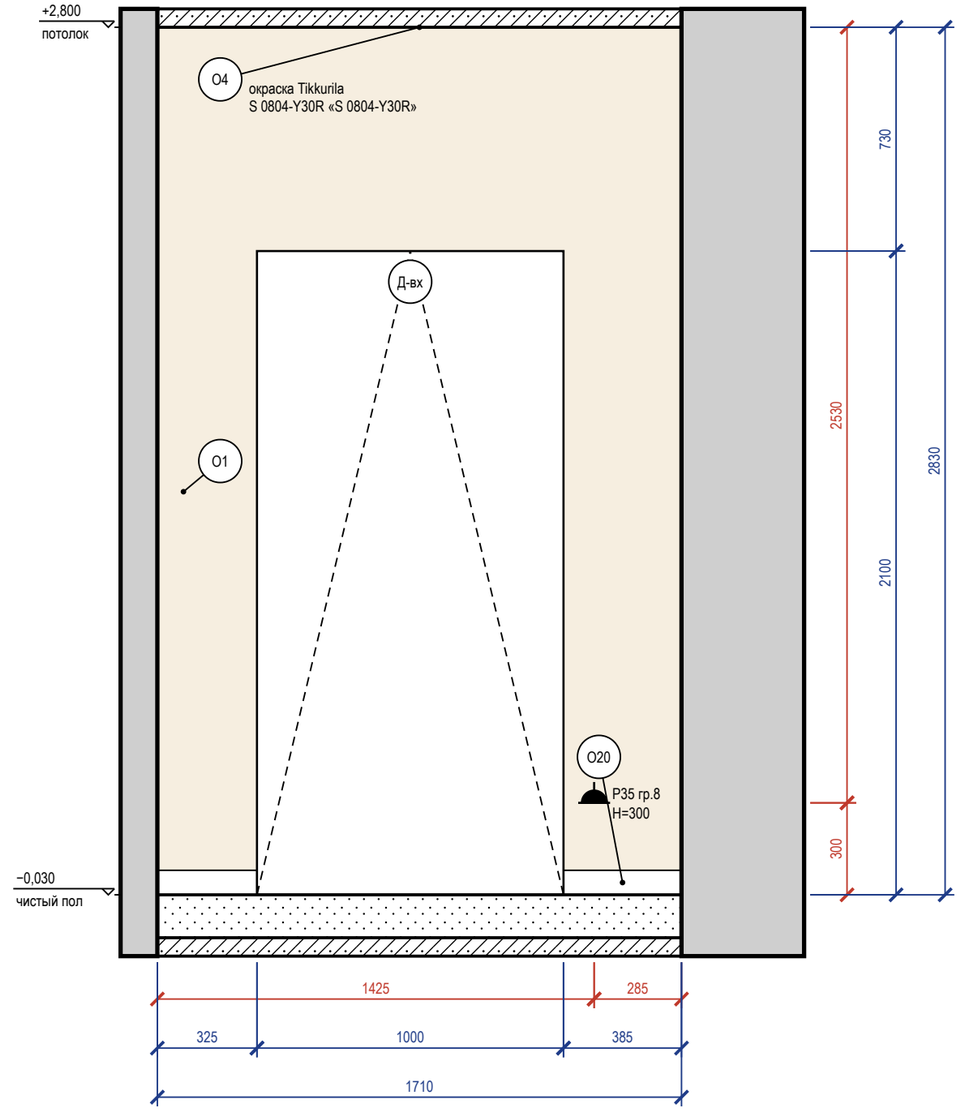


## Схема развёрток (М 1:100)

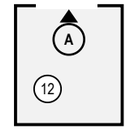


## Ведомость отделки (на листе)

| Марка | Поверхность | Материал, изделие | Цвет, код | Кол. |
|---|---|---|---|---|
| О1 | стены | окраска, Tikkurila Luja 7, шелковисто-матовая, подготовка К3 | NCS S 0804-Y30R «S 0804-Y30R» | 2,7 м² |
| О4 | потолок | окраска, Tikkurila Luja 7, матовая, подготовка Q3 | NCS S 0804-Y30R «S 0804-Y30R» | 3,4 м² |
| О20 | плинтус | керамогранит, аналог: плинтус из керамогранита пола, подрезка 80 мм, верхняя кромка с запилом 45° | #B8AFA5 «тон Claystone V486» | 0,7 м |

## Примечания

1. Размеры — в мм от чистовых поверхностей стен; условные обозначения и общие указания — лист 2.

| | | | | | |
|---|---|---|---|---|---|
| | | | | | Проект: Дом 331 м² |
| | Лист | № док. | Подпись | Дата | Развёртки стен. Крыльцо (пом. 12) |
| Дизайнер | Кырлан А.С. | | | 19.10.26 | |

| Стадия | Лист | Листов |
|---|---|---|
| П | 101 | 156 |

выпуск 18.10.2026 № 8cd922c868 · стр. 101 из 156

Правка к этому листу

| | | | | | | |
|---|---|---|---|---|---|---|
| | | | | | Проект: Дом 331 м² | |
| | Лист | № док. | Подпись | Дата | Визуализация: Спальня мастер | Стадия / Лист / Листов |
| Дизайнер | Кырлан А.С. | | | 19.10.26 | | П / 102 / 156 |

выпуск 18.10.2026 № 8cd922c868 · стр. 102 из 156

Правка к этому листу

| | | | | | |
|---|---|---|---|---|---|
| | | | | | Проект: Дом 331 м² |
| | Лист | № док. | Подпись | Дата | Визуализация: Спальня мастер |
| Дизайнер | Кырлан А.С. | | | 19.10.26 | |

| Стадия | Лист | Листов |
|---|---|---|
| П | 103 | 156 |

выпуск 18.10.2026 № 8cd922c868 · стр. 103 из 156

Правка к этому листу

## Развёртка стены А

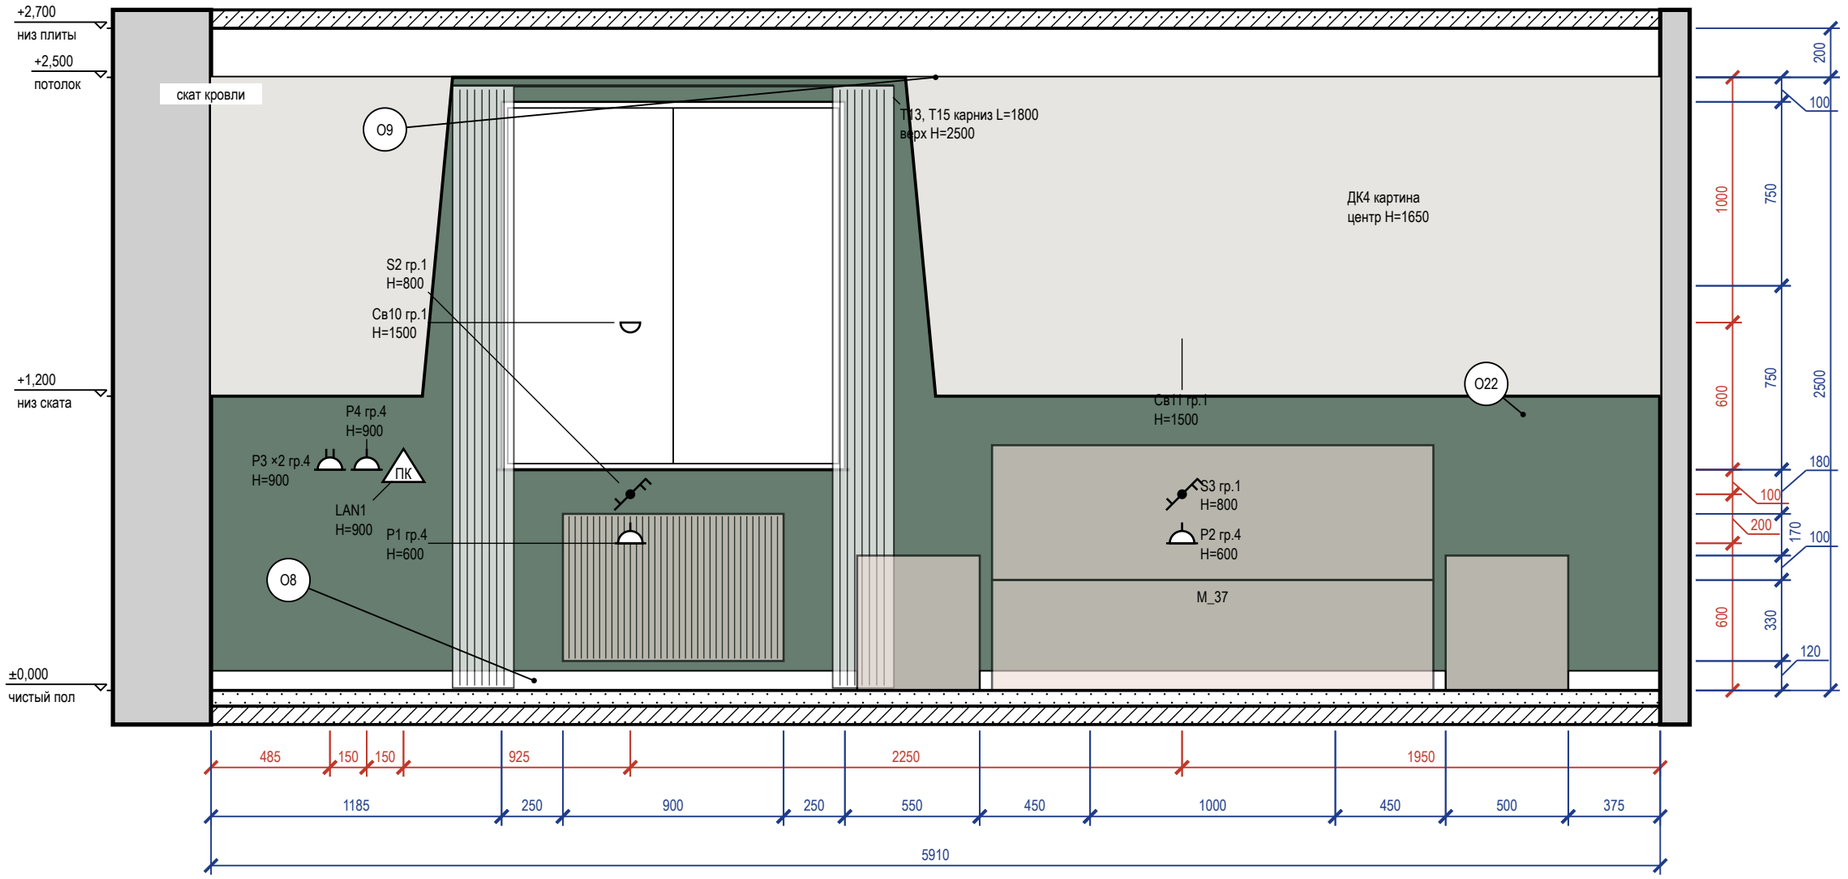


### Схема развёрток (М 1:100)

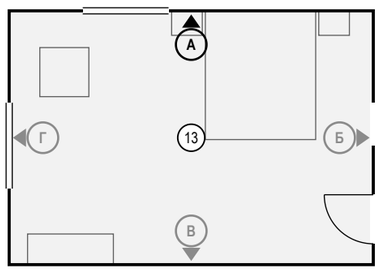


### Ведомость отделки (на листе)

| Марка | Поверхность | Материал, изделие | Цвет, код | Кол. |
|---|---|---|---|---|
| О8 | плинтус | плинтус МДФ, h 80 мм, аналог: плинтус МДФ под покраску 80×16 | Farrow & Ball No. 226 «Joa's White» | 4,9 м |
| О9 | потолок | окраска, Tikkurila Anti-Reflex 2, глубокоматовая, подготовка Q3 | Little Greene No. 105 «Slaked Lime» | 24,6 м² |
| О22 | акцентная стена | окраска, Farrow & Ball Modern Emulsion, матовая, подготовка Q3 | NCS S 7020-G10Y «Хвойный тёмно-зелёный» | 12,7 м² |

Визуализация этой стены

### Примечания

1. Размеры — в мм от чистовых поверхностей стен; условные обозначения и общие указания — лист 2.
2. Картины и зеркала крепить к основанию по паспорту изделия (закладные и анкеры — в перечне скрытых работ); крест — ось центра предмета.
3. Карнизы (шины) — по ведомости текстиля декоратора; длина L и верх Н — по развёртке, крепление — до окраски потолка.
4. Потолок на развёртках — по нижнему уровню У1; другие уровни потолка помещения: У2 +2,600.

| | | | | | |
|---|---|---|---|---|---|
| | | | | | Проект: Дом 331 м² |
| | Лист | № док. | Подпись | Дата | Развёртка стены А. Спальня мастер (пом. 13) |
| Дизайнер | Кырлан А.С. | | | 19.10.26 | |

| Стадия | Лист | Листов |
|---|---|---|
| П | 104 | 156 |

выпуск 18.10.2026 № 8cd922c868 · стр. 104 из 156

Правка к этому листу

## Развёртка стены Б

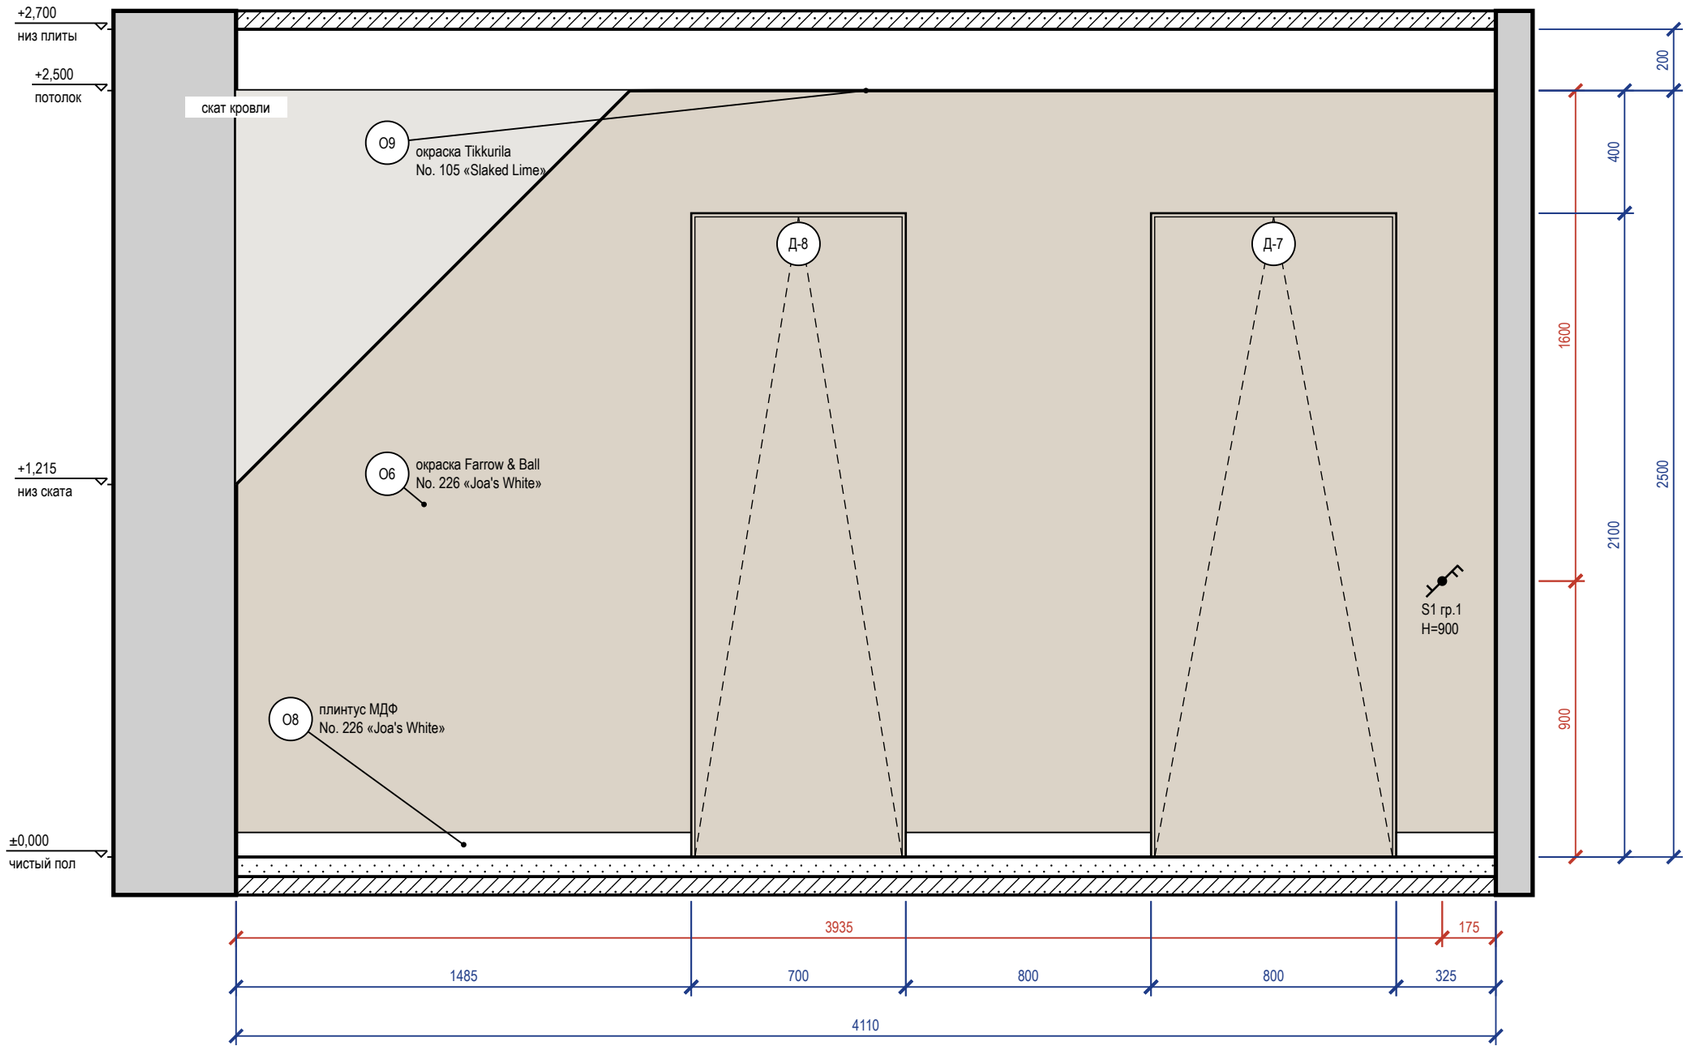


## Схема развёрток (М 1:100)

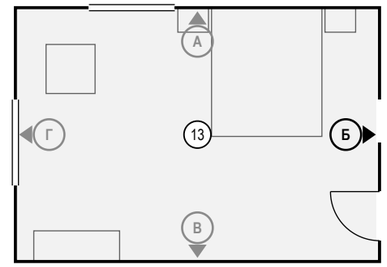


## Ведомость отделки (на листе)

| Марка | Поверхность | Материал, изделие | Цвет, код | Кол. |
|---|---|---|---|---|
| О6 | стены | окраска, Farrow & Ball Modern Emulsion, матовая, подготовка Q3 | Farrow & Ball No. 226 «Joa's White» | 7,1 м² |
| О8 | плинтус | плинтус МДФ, h 80 мм, аналог: плинтус МДФ под покраску 80×16 | Farrow & Ball No. 226 «Joa's White» | 2,6 м |
| О9 | потолок | окраска, Tikkurila Anti-Reflex 2, глубокоматовая, подготовка Q3 | Little Greene No. 105 «Slaked Lime» | 24,6 м² |

## Примечания

1. Размеры — в мм от чистовых поверхностей стен; условные обозначения и общие указания — лист 2.
2. Двери скрытого монтажа — полотно в плоскости стены, отделка стены по полотну, плинтус прерывается у короба (узел — на листе узлов).
3. Потолок на развёртках — по нижнему уровню У1; другие уровни потолка помещения: У2 +2,600.

| | | | | |
|---|---|---|---|---|
| | Лист | № док. | Подпись | Дата |
| Дизайнер | Кырлан А.С. | | | 19.10.26 |

Проект: Дом 331 м²

Развёртка стены Б. Спальня мастер (пом. 13)

| Стадия | Лист | Листов |
|---|---|---|
| П | 105 | 156 |

выпуск 18.10.2026 № 8cd922c868 · стр. 105 из 156

Правка к этому листу

## Развёртка стены В

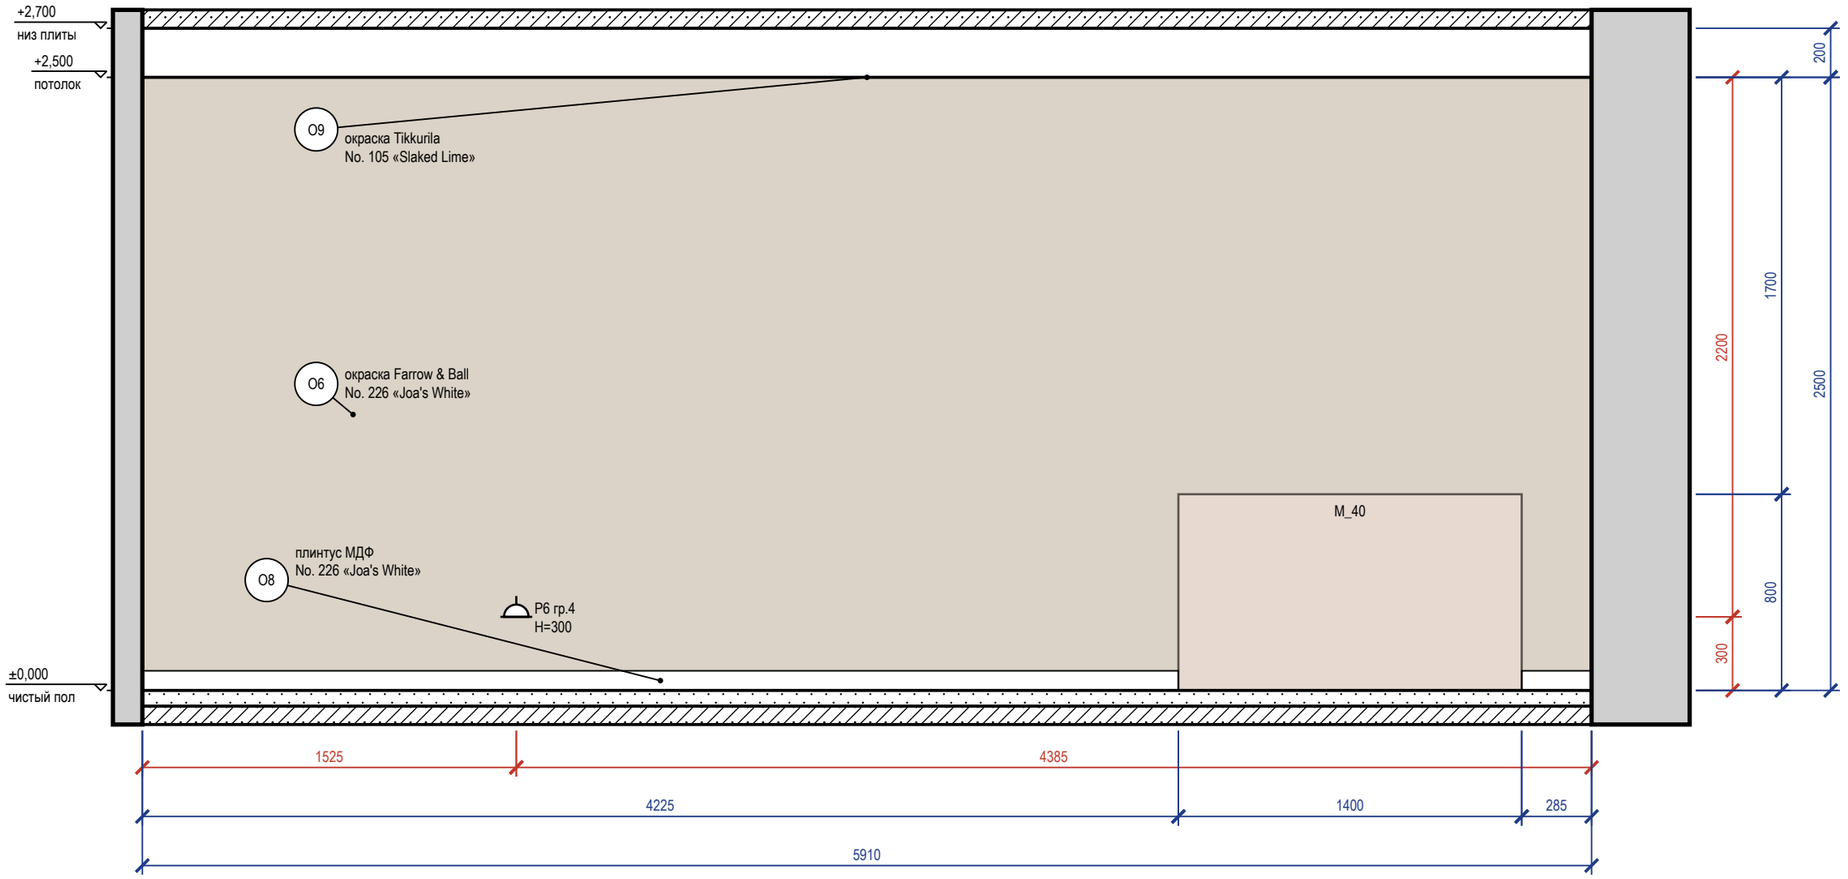


### Схема развёрток (М 1:100)

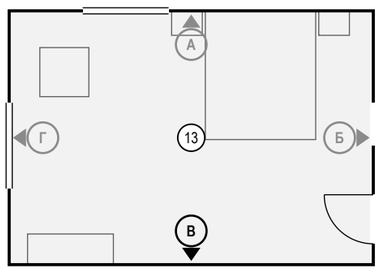


### Ведомость отделки (на листе)

| Марка | Поверхность | Материал, изделие | Цвет, код | Кол. |
|---|---|---|---|---|
| О6 | стены | окраска, Farrow & Ball Modern Emulsion, матовая, подготовка Q3 | Farrow & Ball No. 226 «Joa's White» | 14,8 м² |
| О8 | плинтус | плинтус МДФ, h 80 мм, аналог: плинтус МДФ под покраску 80×16 | Farrow & Ball No. 226 «Joa's White» | 4,5 м |
| О9 | потолок | окраска, Tikkurila Anti-Reflex 2, глубокоматовая, подготовка Q3 | Little Greene No. 105 «Slaked Lime» | 24,6 м² |

Визуализация этой стены — лист 103

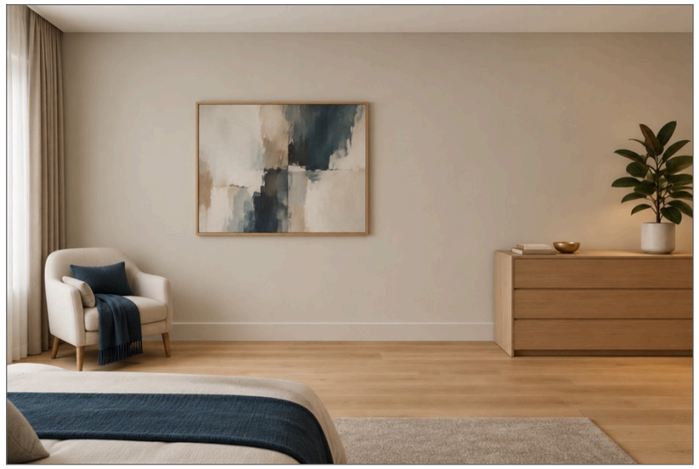

### Примечания

1. Размеры — в мм от чистовых поверхностей стен; условные обозначения и общие указания — лист 2.
2. Потолок на развёртках — по нижнему уровню У1; другие уровни потолка помещения: У2 +2,600.

| | | | | | |
|---|---|---|---|---|---|
| | | | | | Проект: Дом 331 м² |
| | Лист | № док. | Подпись | Дата | |
| Дизайнер | Кырлан А.С. | | | 19.10.26 | Развёртка стены В. Спальня мастер (пом. 13) |

| Стадия | Лист | Листов |
|---|---|---|
| П | 106 | 156 |

выпуск 18.10.2026 № 8cd922c868 · стр. 106 из 156

Правка к этому листу

## Развёртка стены Г

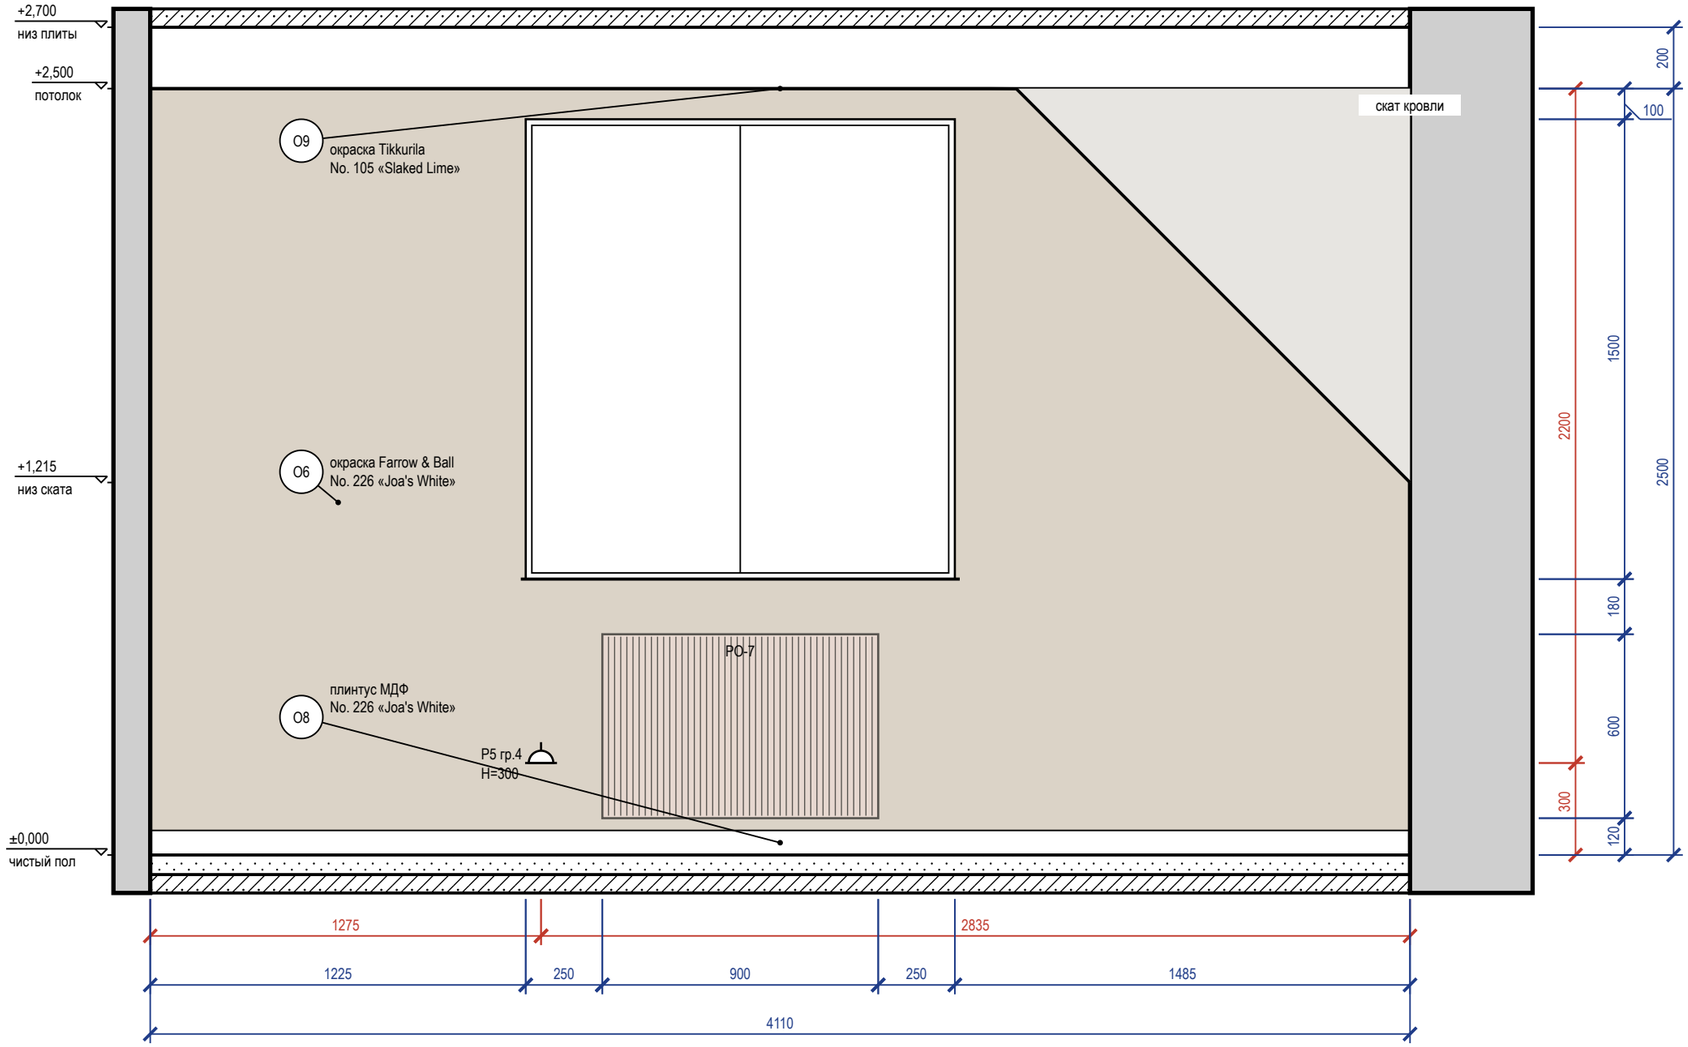


## Схема развёрток (М 1:100)

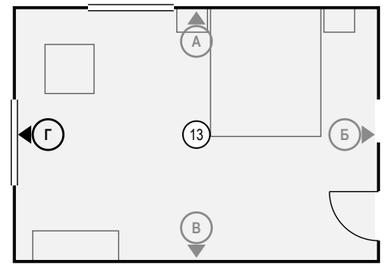


Визуализация этой стены

## Ведомость отделки (на листе)

| Марка | Поверхность | Материал, изделие | Цвет, код | Кол. |
|---|---|---|---|---|
| О6 | стены | окраска, Farrow & Ball Modern Emulsion, матовая, подготовка Q3 | Farrow & Ball No. 226 «Joa's White» | 8,2 м² |
| О8 | плинтус | плинтус МДФ, h 80 мм, аналог: плинтус МДФ под покраску 80×16 | Farrow & Ball No. 226 «Joa's White» | 4,1 м |
| О9 | потолок | окраска, Tikkurila Anti-Reflex 2, глубокоматовая, подготовка Q3 | Little Greene No. 105 «Slaked Lime» | 24,6 м² |

## Примечания

1. Размеры — в мм от чистовых поверхностей стен; условные обозначения и общие указания — лист 2.
2. Потолок на развёртках — по нижнему уровню У1; другие уровни потолка помещения: У2 +2,600.

| | | | | | |
|---|---|---|---|---|---|
| | | | | | Проект: Дом 331 м² |
| | Лист | № док. | Подпись | Дата | Развёртка стены Г. Спальня мастер (пом. 13) |
| Дизайнер | Кырлан А.С. | | | 19.10.26 | |

| Стадия | Лист | Листов |
|---|---|---|
| П | 107 | 156 |

выпуск 18.10.2026 № 8cd922c868 · стр. 107 из 156

Правка к этому листу

| | | | | | |
|---|---|---|---|---|---|
| | | | | | Проект: Дом 331 м² |
| | Лист | № док. | Подпись | Дата | |
| Дизайнер | Кырлан А.С. | | | 19.10.26 | Визуализация: Гардеробная мастер |

| Стадия | Лист | Листов |
|---|---|---|
| П | 108 | 156 |

выпуск 18.10.2026 № 8cd922c868 · стр. 108 из 156

## Развёртка стены А

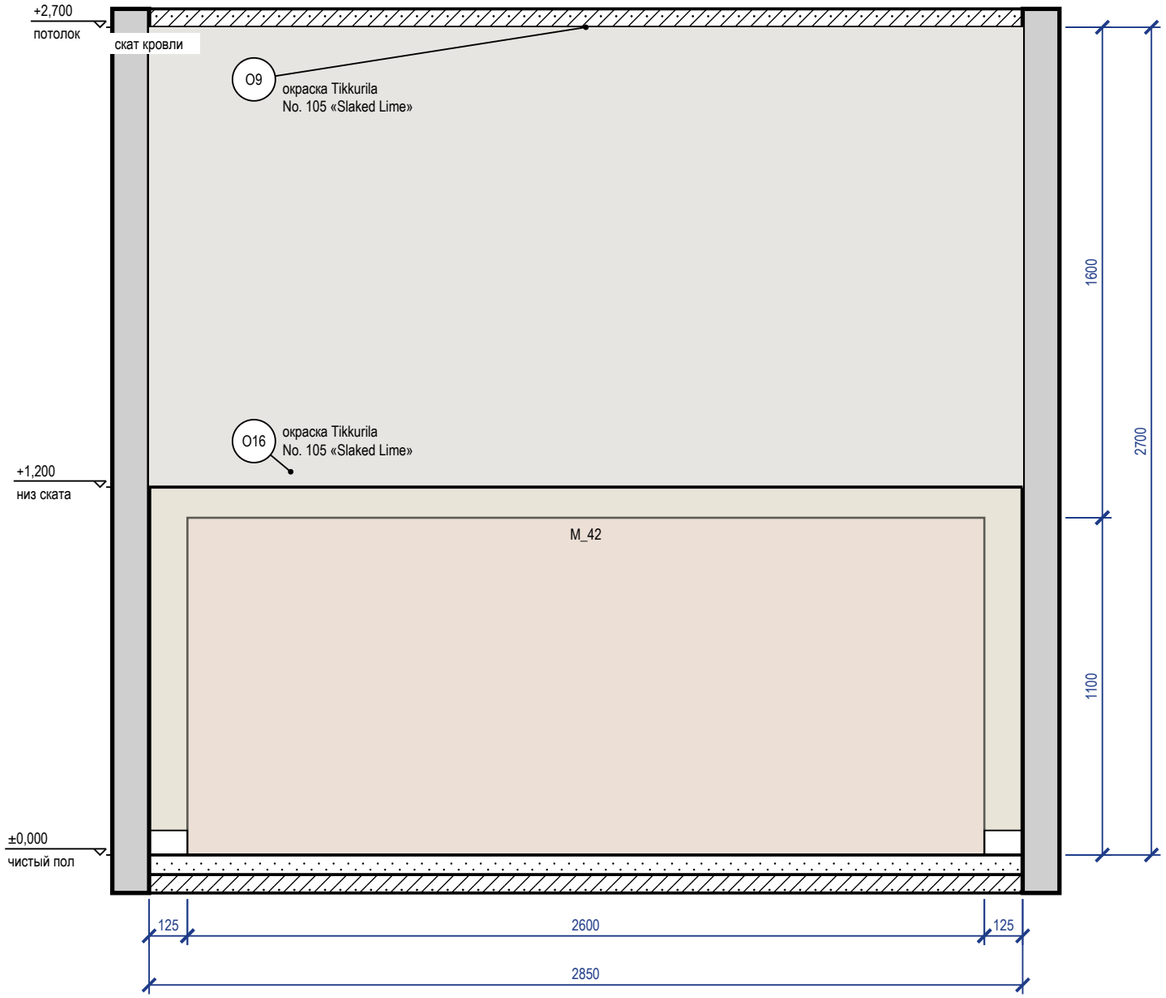


## Развёртка стены Б

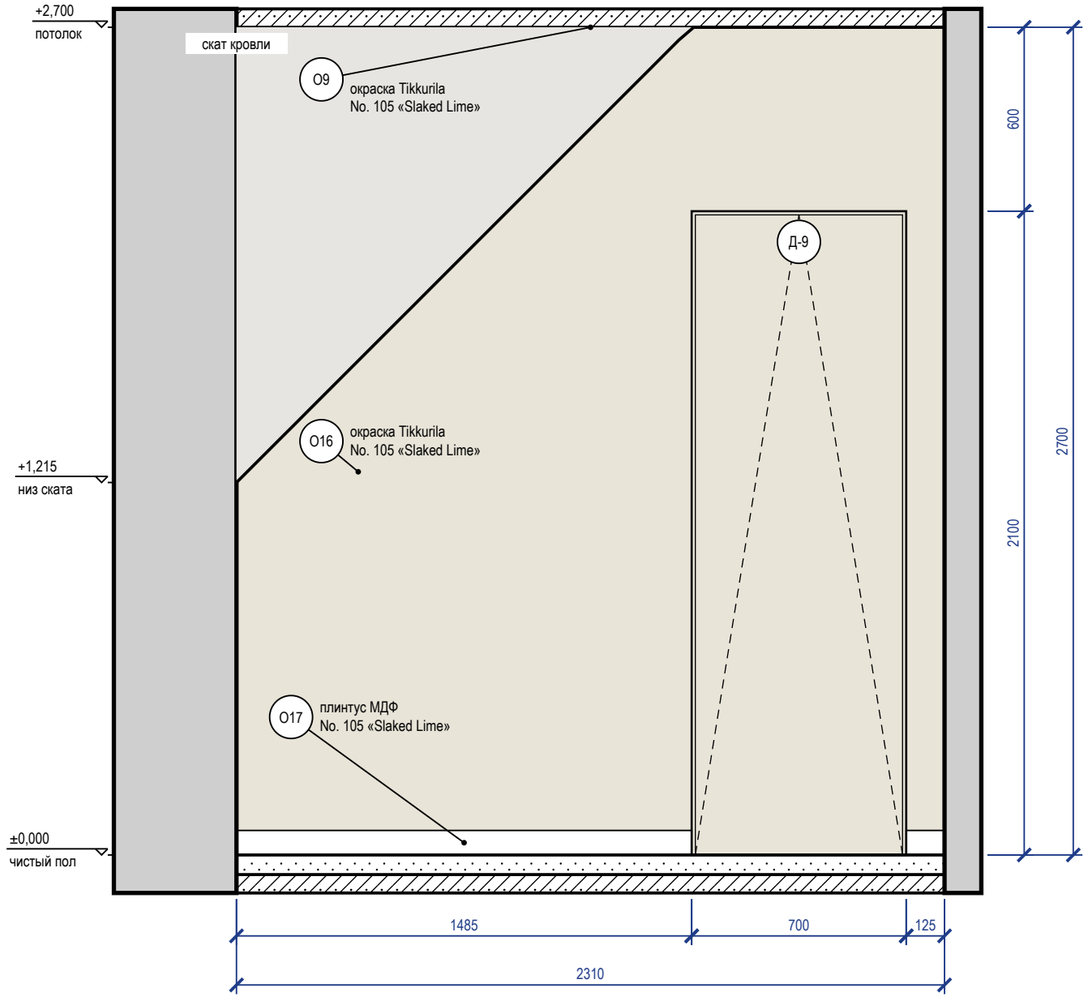


### Схема развёрток (М 1:100)

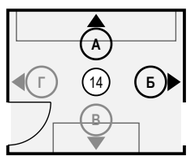


### Ведомость отделки (на листе)

| Марка | Поверхность | Материал, изделие | Цвет, код | Кол. |
|---|---|---|---|---|
| О9 | потолок | окраска, Tikkurila Anti-Reflex 2, глубокоматовая, подготовка Q3 | Little Greene No. 105 «Slaked Lime» | 6,7 м² |
| О16 | стены | окраска, Tikkurila Harmony, матовая, подготовка Q3 | Little Greene No. 105 «Slaked Lime» | 12,5 м² |
| О17 | плинтус | плинтус МДФ, h 80 мм, аналог: плинтус МДФ под покраску 80×16 | Little Greene No. 105 «Slaked Lime» | 1,9 м |

Визуализация этой стены

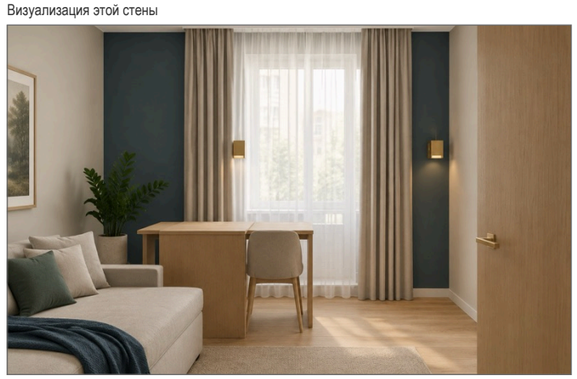

### Примечания

1. Размеры — в мм от чистовых поверхностей стен; условные обозначения и общие указания — лист 2.
2. Двери скрытого монтажа — полотно в плоскости стены, отделка стены по полотну, плинтус прерывается у короба (узел — на листе узлов).

| | | | | |
|---|---|---|---|---|
| | Лист | № док. | Подпись | Дата |
| Дизайнер | Кырлан А.С. | | | 19.10.26 |

Проект: Дом 331 м²

Развёртки стен А, Б. Гардеробная мастер (пом. 14)

| Стадия | Лист | Листов |
|---|---|---|
| П | 109 | 156 |

выпуск 18.10.2026 № 8cd922c868 · стр. 109 из 156

Правка к этому листу

## Развёртка стены В

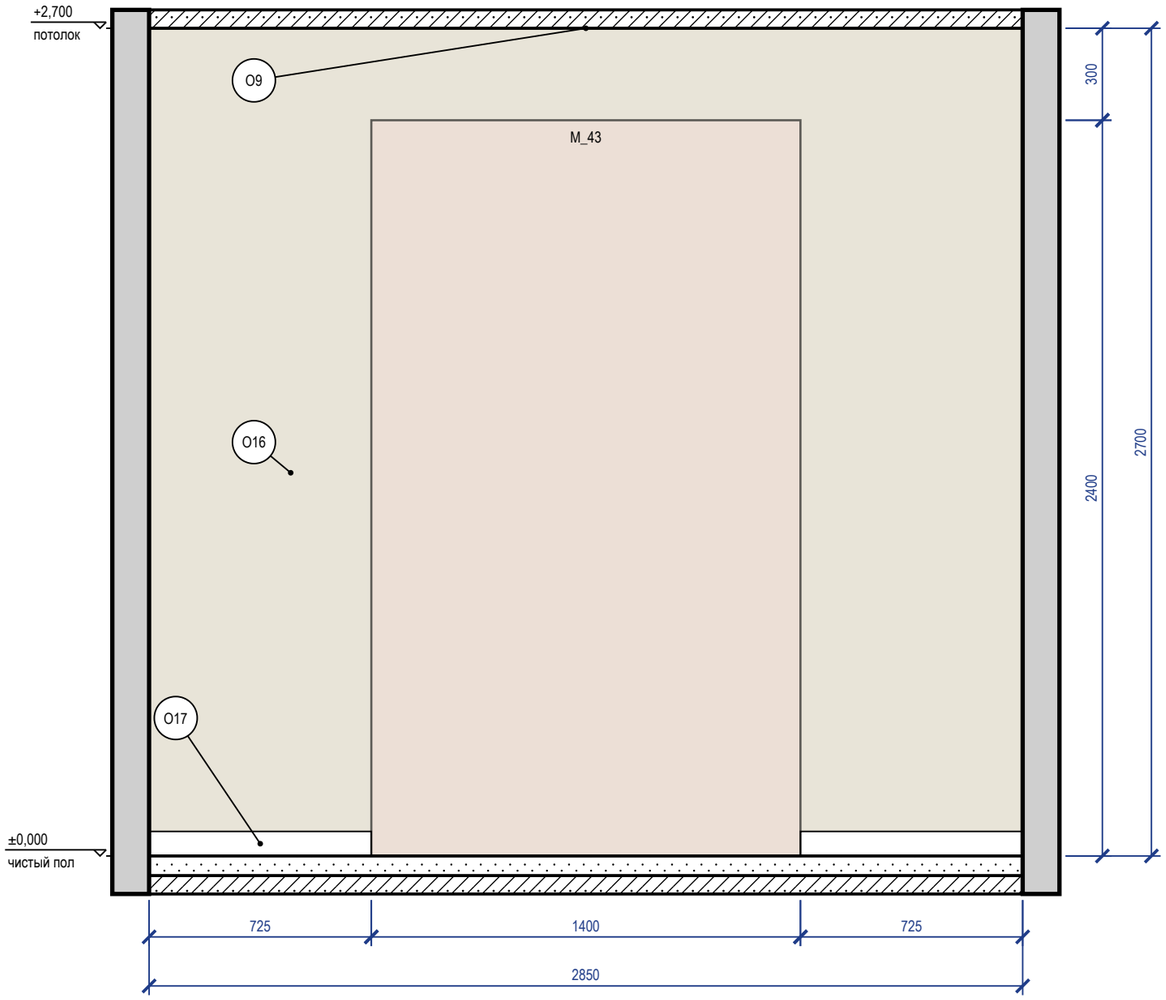


## Развёртка стены Г

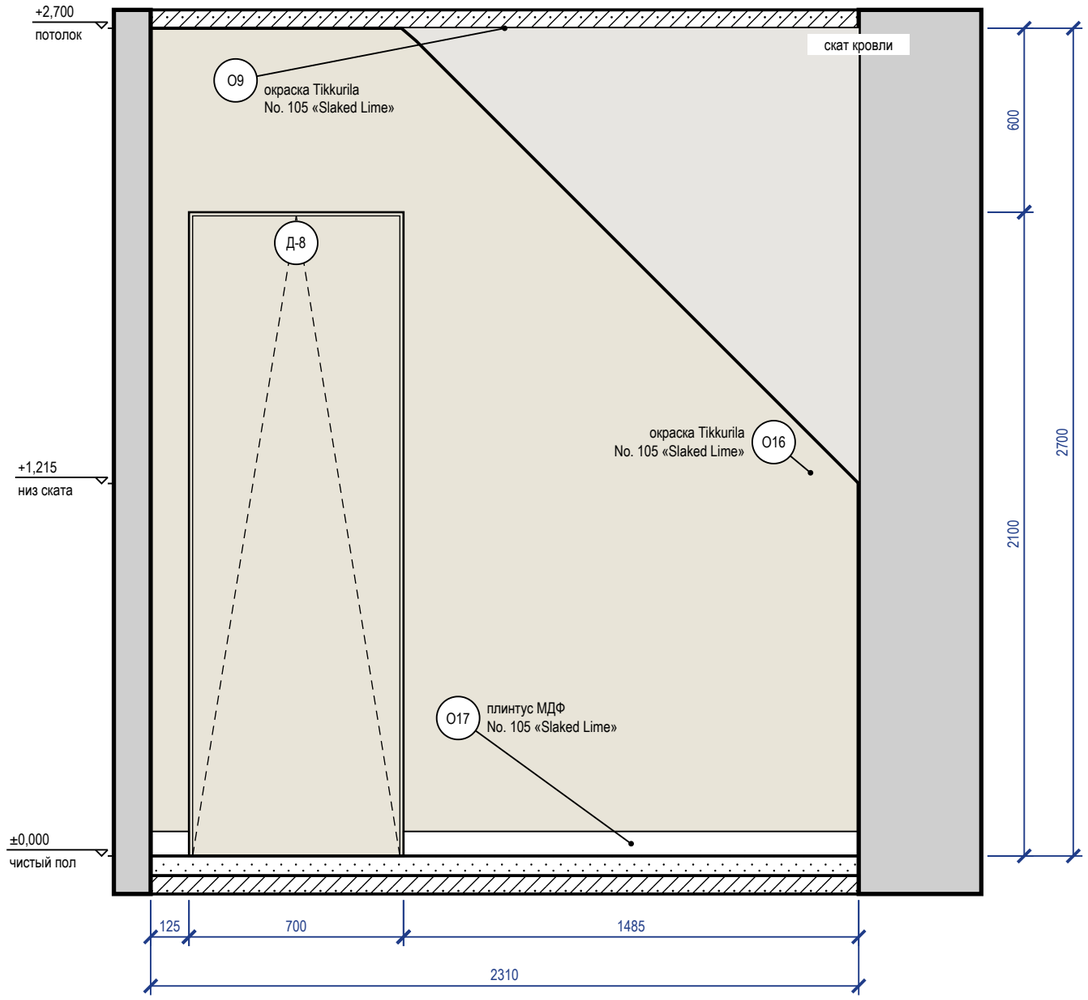


### Схема развёрток (М 1:100)

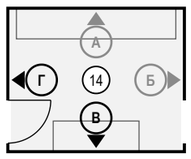


### Ведомость отделки (на листе)

| Марка | Поверхность | Материал, изделие | Цвет, код | Кол. |
|---|---|---|---|---|
| О9 | потолок | окраска, Tikkurila Anti-Reflex 2, глубокоматовая, подготовка Q3 | Little Greene No. 105 «Slaked Lime» | 6,7 м² |
| О16 | стены | окраска, Tikkurila Harmony, матовая, подготовка Q3 | Little Greene No. 105 «Slaked Lime» | 12,5 м² |
| О17 | плинтус | плинтус МДФ, h 80 мм, аналог: плинтус МДФ под покраску 80×16 | Little Greene No. 105 «Slaked Lime» | 3,1 м |

Визуализация этой стены

### Примечания

1. Размеры — в мм от чистовых поверхностей стен; условные обозначения и общие указания — лист 2.
2. Двери скрытого монтажа — полотно в плоскости стены, отделка стены по полотну, плинтус прерывается у короба (узел — на листе узлов).

| | | | | | |
|---|---|---|---|---|---|
| | | | | | Проект: Дом 331 м² |
| | Лист | № док. | Подпись | Дата | Развёртки стен В, Г. Гардеробная мастер (пом. 14) |
| Дизайнер | Кырлан А.С. | | | 19.10.26 | |

| Стадия | Лист | Листов |
|---|---|---|
| П | 110 | 156 |

выпуск 18.10.2026 № 8cd922c868 · стр. 110 из 156

Правка к этому листу

| | | | | | |
|---|---|---|---|---|---|
| | | | | | Проект: Дом 331 м² |
| | Лист | № док. | Подпись | Дата | |
| Дизайнер | Кырлан А.С. | | | 19.10.26 | Визуализация: Санузел мастер |

| Стадия | Лист | Листов |
|---|---|---|
| П | 111 | 156 |

выпуск 18.10.2026 № 8cd922c868 · стр. 111 из 156

Правка к этому листу

## Развёртка стены А

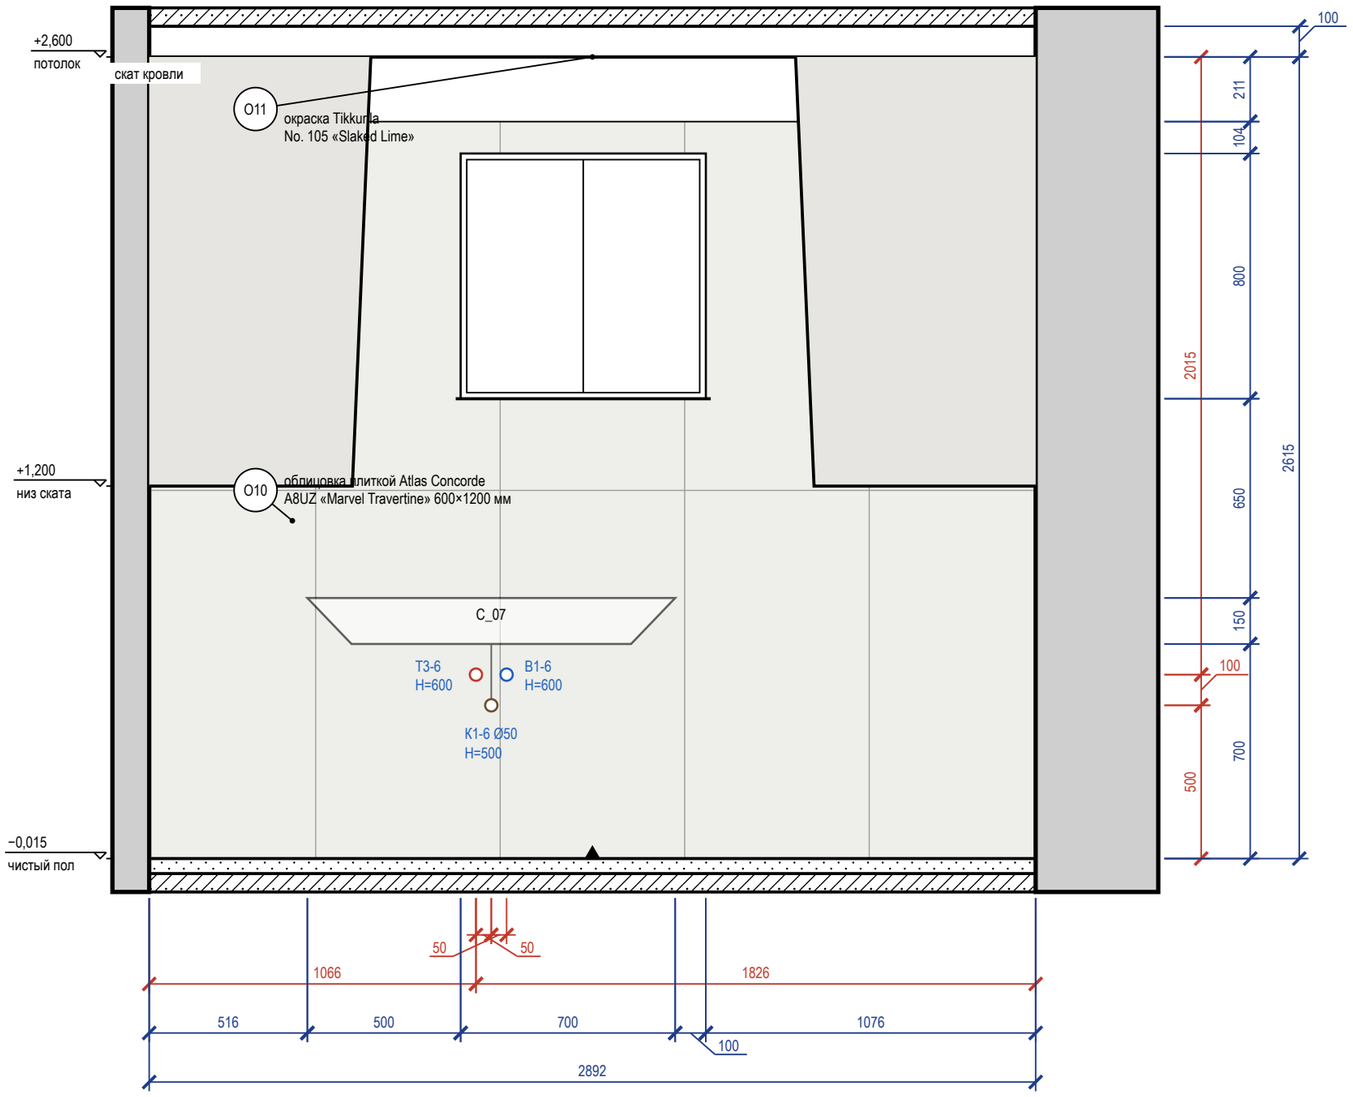


## Схема развёрток (М 1:100)

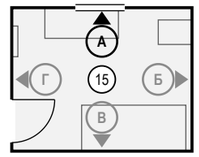


## Ведомость отделки (на листе)

| Марка | Поверхность | Материал, изделие | Цвет, код | Кол. |
|---|---|---|---|---|
| О10 | стены | облицовка плиткой, Atlas Concorde Marvel Travertine, 600×1200×9 мм, A8UZ, затирка CG2WA | Atlas Concorde A8UZ «Marvel Travertine» | 6,3 м² |
| О11 | потолок | окраска, Tikkurila Luja 7, матовая, подготовка Q3 | Little Greene No. 105 «Slaked Lime» | 6,9 м² |

## Примечания

1. Размеры — в мм от чистовых поверхностей стен; условные обозначения и общие указания — лист 2.
2. Схема мебели, приборов и декора не является технической документацией для производства мебели; габариты — по паспортам изделий.
3. Выводы ВК — коды и высоты по листу выводов сантехники.
4. Облицовка — по сетке швов 2 мм, раскладка от оси стены (треугольник у пола), целые ряды от пола; подрезки — по листу раскладки плитки.
5. Гидроизоляция в 2 слоя, заход на стены 200 мм — до облицовки, с актом скрытых работ и тестом проливом (узел — на листе узлов).

| | | | | | |
|---|---|---|---|---|---|
| | | | | | Проект: Дом 331 м² |
| | Лист | № док. | Подпись | Дата | Развёртка стены А. Санузел мастер (пом. 15) |
| Дизайнер | Кырлан А.С. | | | 19.10.26 | |

| Стадия | Лист | Листов |
|---|---|---|
| П | 112 | 156 |

выпуск 18.10.2026 № 8cd922c868 · стр. 112 из 156

Правка к этому листу

## Развёртка стены Б

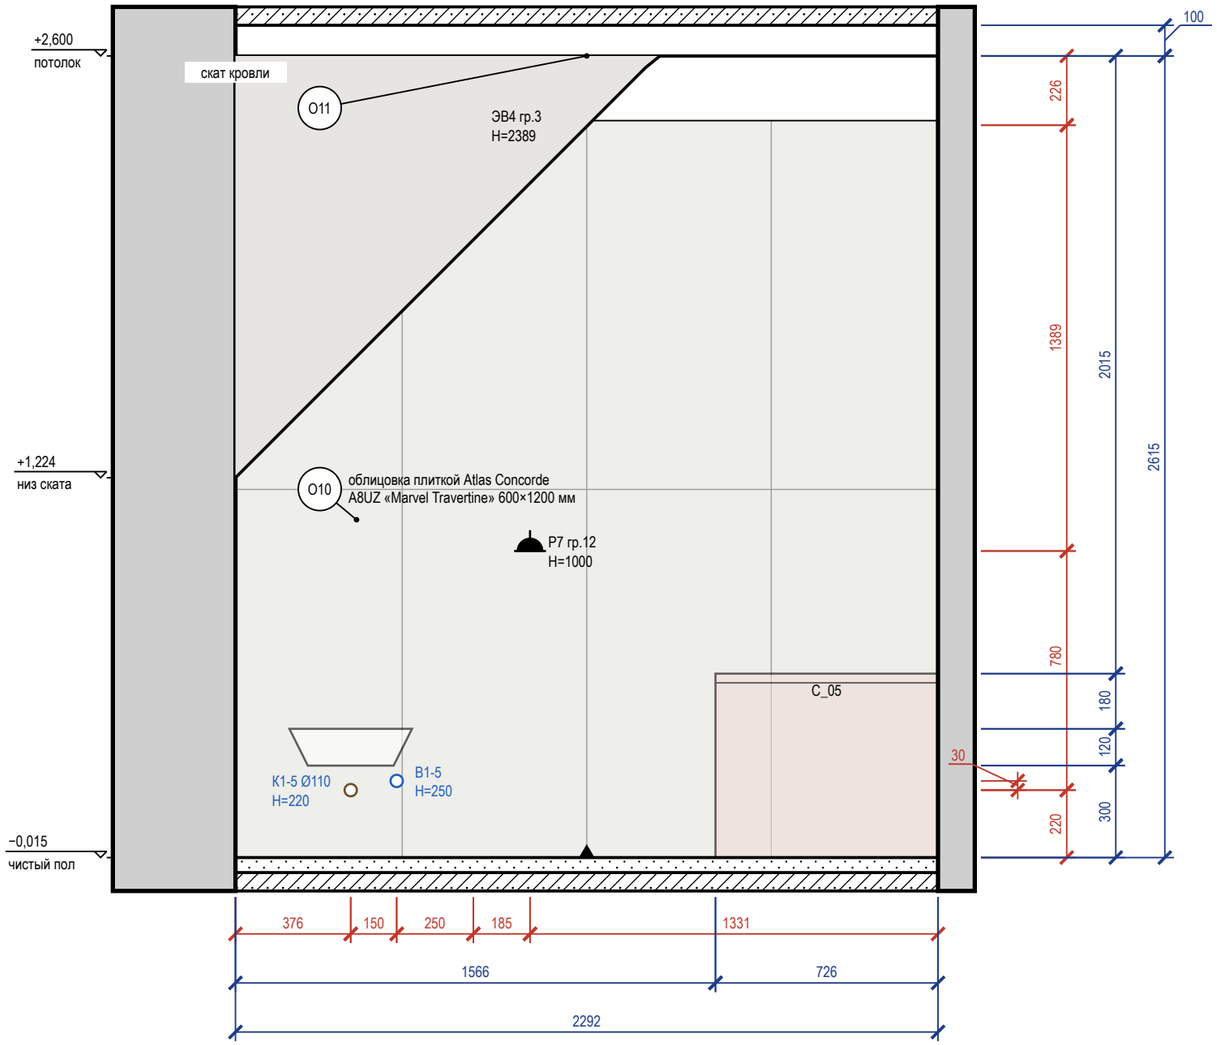


## Схема развёрток (М 1:100)

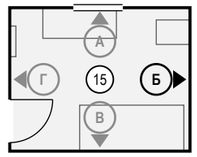


## Ведомость отделки (на листе)

| Марка | Поверхность | Материал, изделие | Цвет, код | Кол. |
|---|---|---|---|---|
| О10 | стены | облицовка плиткой, Atlas Concorde Marvel Travertine, 600×1200×9 мм, A8UZ, затирка CG2WA | Atlas Concorde A8UZ «Marvel Travertine» | 5,5 м² |
| О11 | потолок | окраска, Tikkurila Luja 7, матовая, подготовка Q3 | Little Greene No. 105 «Slaked Lime» | 6,9 м² |

Визуализация этой стены — лист 111

## Примечания

1. Размеры — в мм от чистовых поверхностей стен; условные обозначения и общие указания — лист 2.
2. Схема мебели, приборов и декора не является технической документацией для производства мебели; габариты — по паспортам изделий.
3. Выводы ВК — коды и высоты по листу выводов сантехники.
4. Облицовка — по сетке швов 2 мм, раскладка от оси стены (треугольник у пола), целые ряды от пола; подрезки — по листу раскладки плитки.
5. Гидроизоляция в 2 слоя, заход на стены 200 мм — до облицовки, с актом скрытых работ и тестом проливом (узел — на листе узлов).

| | | | | | |
|---|---|---|---|---|---|
| | | | | | Проект: Дом 331 м² |
| | Лист | № док. | Подпись | Дата | Развёртка стены Б. Санузел мастер (пом. 15) |
| Дизайнер | Кырлан А.С. | | | 19.10.26 | |

| Стадия | Лист | Листов |
|---|---|---|
| П | 113 | 156 |

выпуск 18.10.2026 № 8cd922c868 · стр. 113 из 156

Правка к этому листу

## Развёртка стены В

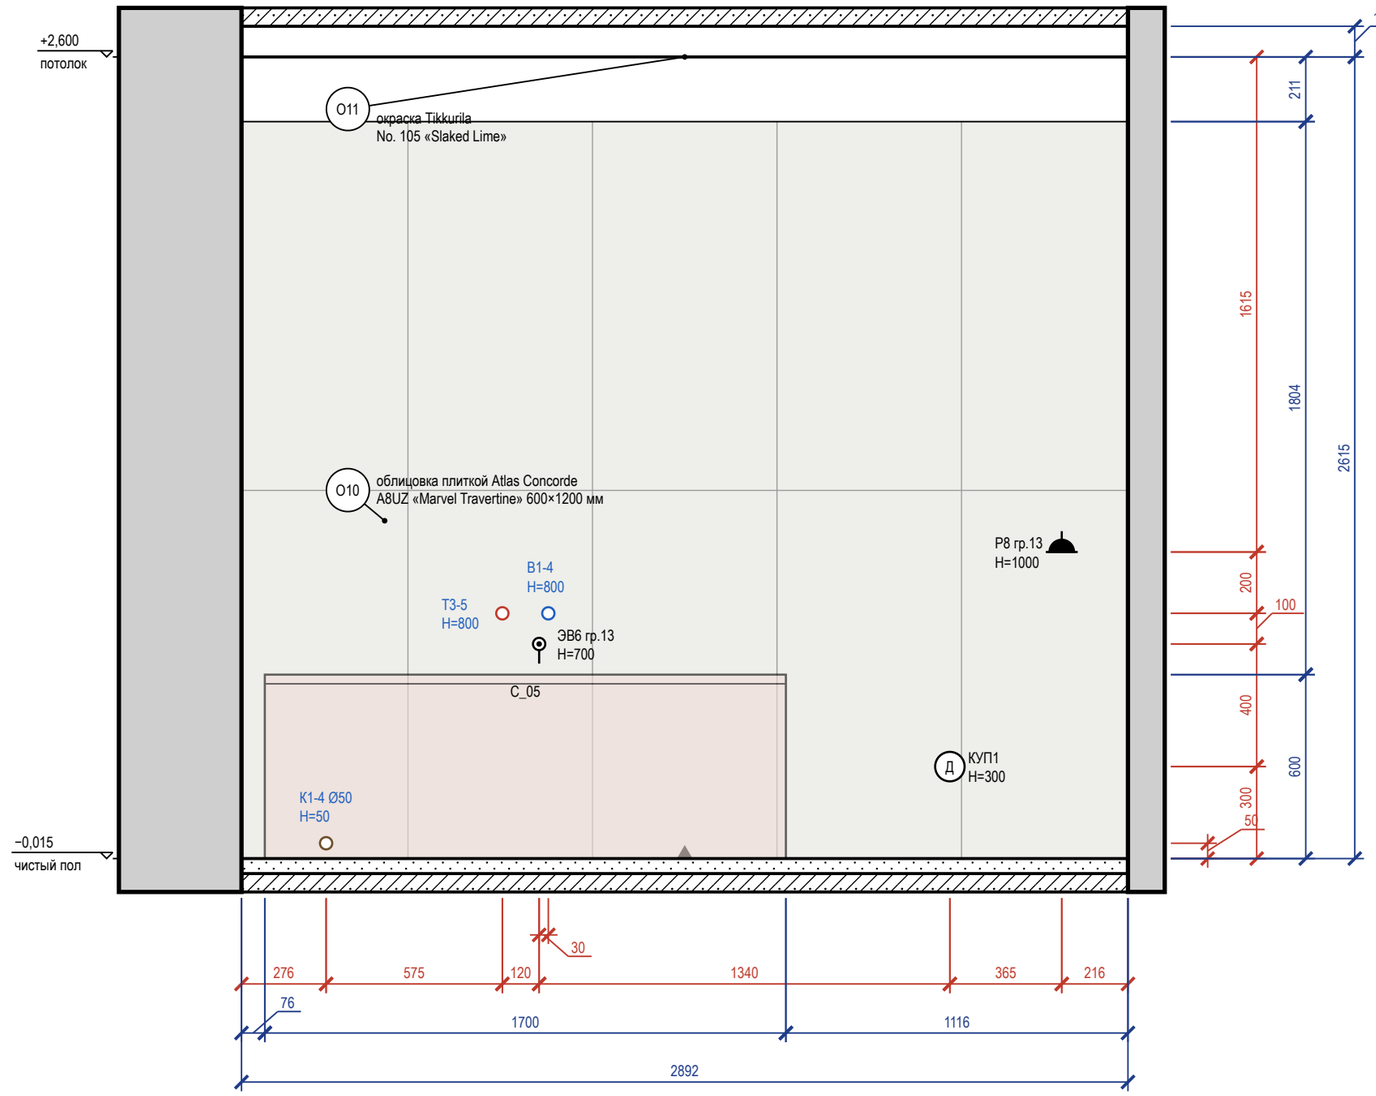


## Схема развёрток (М 1:100)

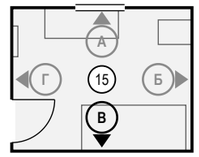


## Ведомость отделки (на листе)

| Марка | Поверхность | Материал, изделие | Цвет, код | Кол. |
|---|---|---|---|---|
| О10 | стены | облицовка плиткой, Atlas Concorde Marvel Travertine, 600×1200×9 мм, A8UZ, затирка CG2WA | Atlas Concorde A8UZ «Marvel Travertine» | 7 м² |
| О11 | потолок | окраска, Tikkurila Luja 7, матовая, подготовка Q3 | Little Greene No. 105 «Slaked Lime» | 6,9 м² |

## Примечания

1. Размеры — в мм от чистовых поверхностей стен; условные обозначения и общие указания — лист 2.
2. Схема мебели, приборов и декора не является технической документацией для производства мебели; габариты — по паспортам изделий.
3. Выводы ВК — коды и высоты по листу выводов сантехники.
4. Облицовка — по сетке швов 2 мм, раскладка от оси стены (треугольник у пола), целые ряды от пола; подрезки — по листу раскладки плитки.
5. Гидроизоляция в 2 слоя, заход на стены 200 мм — до облицовки, с актом скрытых работ и тестом проливом (узел — на листе узлов).

| | | | | | |
|---|---|---|---|---|---|
| | | | | | Проект: Дом 331 м² |
| | Лист | № док. | Подпись | Дата | Развёртка стены В. Санузел мастер (пом. 15) |
| Дизайнер | Кырлан А.С. | | | 19.10.26 | |

| Стадия | Лист | Листов |
|---|---|---|
| П | 114 | 156 |

выпуск 18.10.2026 № 8cd922c868 · стр. 114 из 156

Правка к этому листу

## Развёртка стены Г

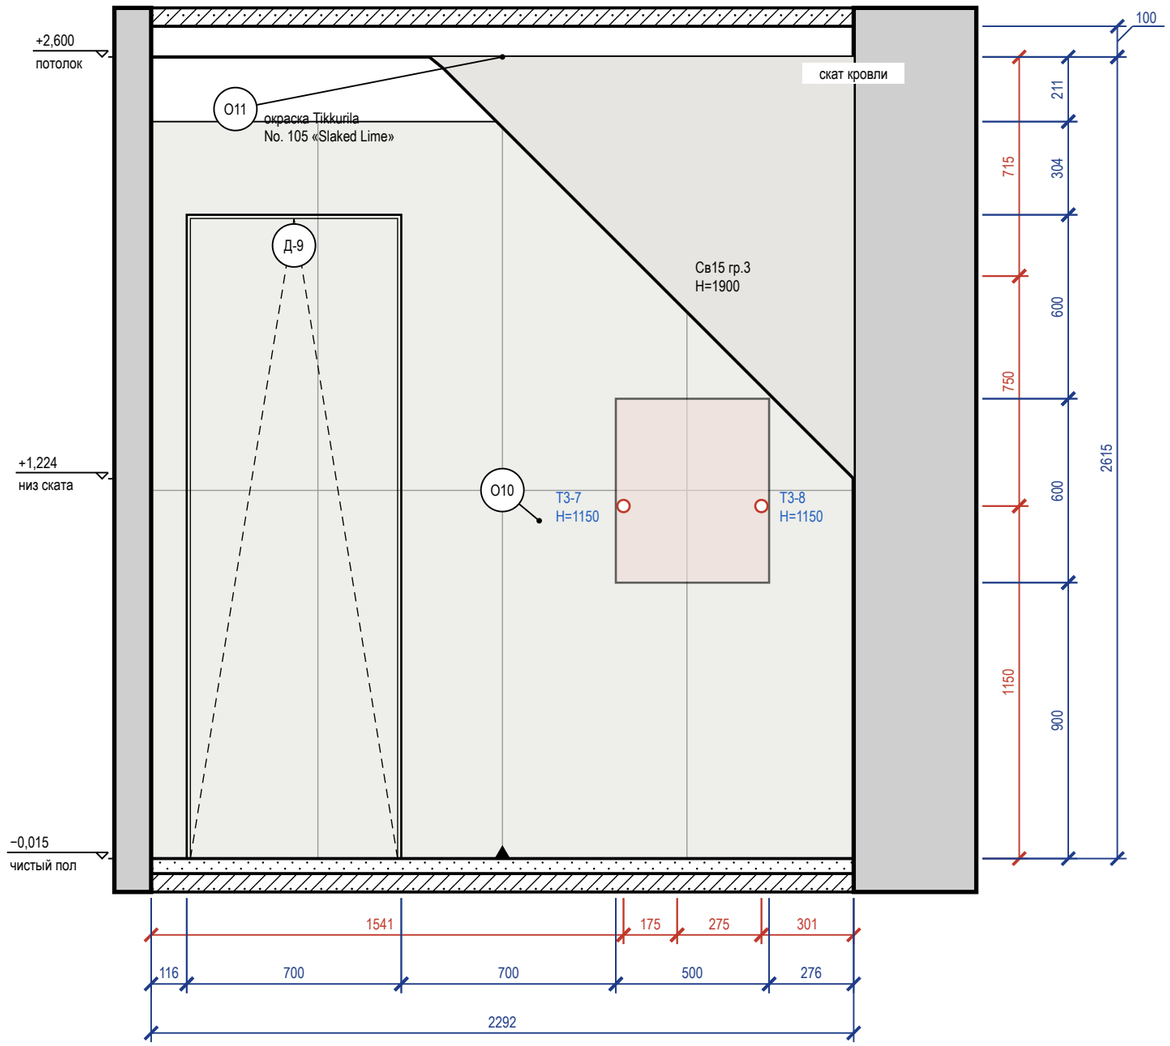


## Схема развёрток (М 1:100)

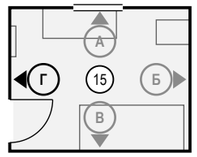


## Ведомость отделки (на листе)

| Марка | Поверхность | Материал, изделие | Цвет, код | Кол. |
|---|---|---|---|---|
| О10 | стены | облицовка плиткой, Atlas Concorde Marvel Travertine, 600×1200×9 мм, A8UZ, затирка CG2WA | Atlas Concorde A8UZ «Marvel Travertine» | 4 м² |
| О11 | потолок | окраска, Tikkurila Luja 7, матовая, подготовка Q3 | Little Greene No. 105 «Slaked Lime» | 6,9 м² |

Визуализация этой стены

## Примечания

1. Размеры — в мм от чистовых поверхностей стен; условные обозначения и общие указания — лист 2.
2. Схема мебели, приборов и декора не является технической документацией для производства мебели; габариты — по паспортам изделий.
3. Выводы ВК — коды и высоты по листу выводов сантехники.
4. Облицовка — по сетке швов 2 мм, раскладка от оси стены (треугольник у пола), целые ряды от пола; подрезки — по листу раскладки плитки.
5. Гидроизоляция в 2 слоя, заход на стены 200 мм — до облицовки, с актом скрытых работ и тестом проливом (узел — на листе узлов).
6. Двери скрытого монтажа — полотно в плоскости стены, отделка стены по полотну, плинтус прерывается у короба (узел — на листе узлов).

| | | | | | |
|---|---|---|---|---|---|
| | | | | | Проект: Дом 331 м² |
| | Лист | № док. | Подпись | Дата | |
| Дизайнер | Кырлан А.С. | | | 19.10.26 | Развёртка стены Г. Санузел мастер (пом. 15) |
| | | | | | Стадия: П; Лист: 115; Листов: 156 |

выпуск 18.10.2026 № 8cd922c868 · стр. 115 из 156

Правка к этому листу

| | | | | | |
|---|---|---|---|---|---|
| | | | | | Проект: Дом 331 м² |
| | Лист | № док. | Подпись | Дата | Визуализация: Спальня 2 |
| Дизайнер | Кырлан А.С. | | | 19.10.26 | |

| Стадия | Лист | Листов |
|---|---|---|
| П | 116 | 156 |

выпуск 18.10.2026 № 8cd922c868 · стр. 116 из 156

Правка к этому листу

| | | | | | | |
|---|---|---|---|---|---|---|
| | | | | | Проект: Дом 331 м² | |
| | Лист | № док. | Подпись | Дата | Визуализация: Спальня 2 | Стадия / Лист / Листов |
| Дизайнер | Кырлан А.С. | | | 19.10.26 | | П / 117 / 156 |

выпуск 18.10.2026 № 8cd922c868 · стр. 117 из 156

Правка к этому листу

## Развёртка стены А

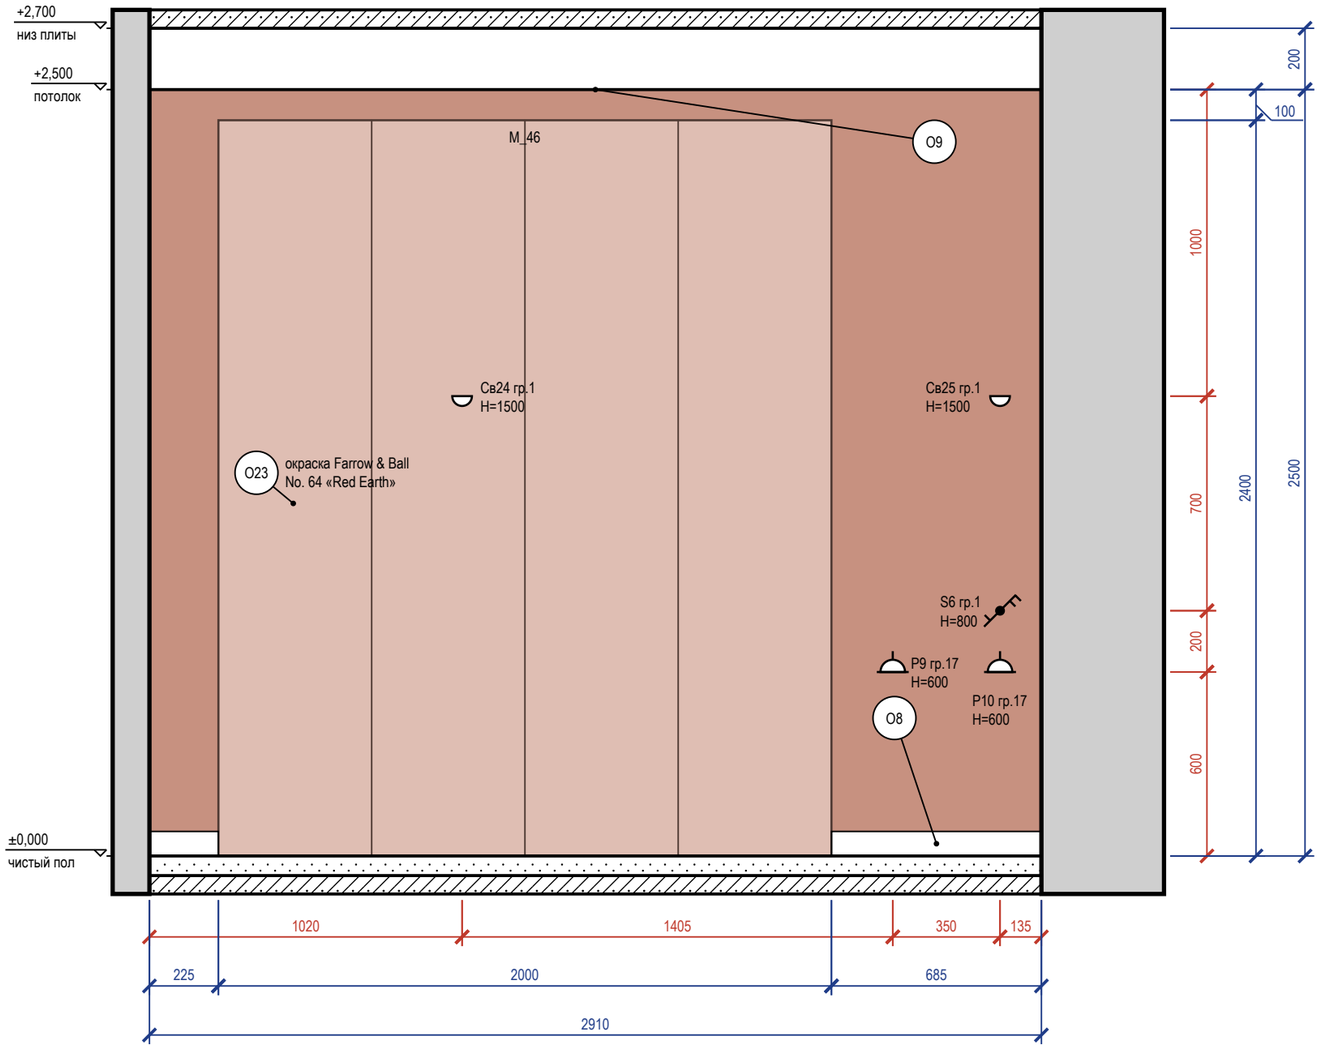


## Схема развёрток (М 1:100)

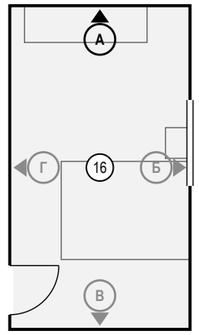


## Ведомость отделки (на листе)

| Марка | Поверхность | Материал, изделие | Цвет, код | Кол. |
|---|---|---|---|---|
| О8 | плинтус | плинтус МДФ, h 80 мм, аналог: плинтус МДФ под покраску 80×16 | Farrow & Ball No. 226 «Joa's White» | 0,9 м |
| О9 | потолок | окраска, Tikkurila Anti-Reflex 2, глубокоматовая, подготовка Q3 | Little Greene No. 105 «Slaked Lime» | 15,5 м² |
| О23 | акцентная стена | окраска, Farrow & Ball Modern Emulsion, матовая, подготовка Q3 | Farrow & Ball No. 64 «Red Earth» | 7,3 м² |

Визуализация этой стены — лист 116

**4** **Короб стояков К1-1 с люком и звукоизоляцией (М 1:20)**

Узел 4 — лист С3

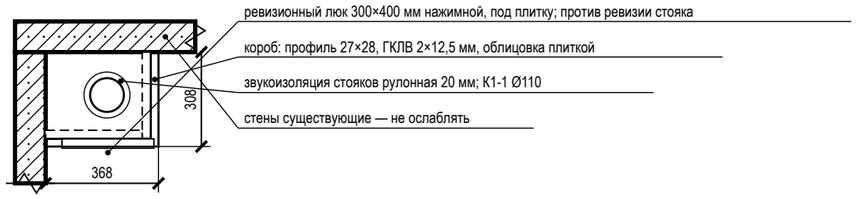


## Примечания

1. Размеры — в мм от чистовых поверхностей стен; условные обозначения и общие указания — лист 2.
2. Потолок на развёртках — по нижнему уровню У1; другие уровни потолка помещения: У2 +2,600.

| | | | | | |
|---|---|---|---|---|---|
| | | | | | Проект: Дом 331 м² |
| | Лист | № док. | Подпись | Дата | Развёртка стены А. Спальня 2 (пом. 16) |
| Дизайнер | Кырлан А.С. | | | 19.10.26 | |

| Стадия | Лист | Листов |
|---|---|---|
| П | 118 | 156 |

выпуск 18.10.2026 № 8cd922c868 · стр. 118 из 156

## Развёртка стены Б

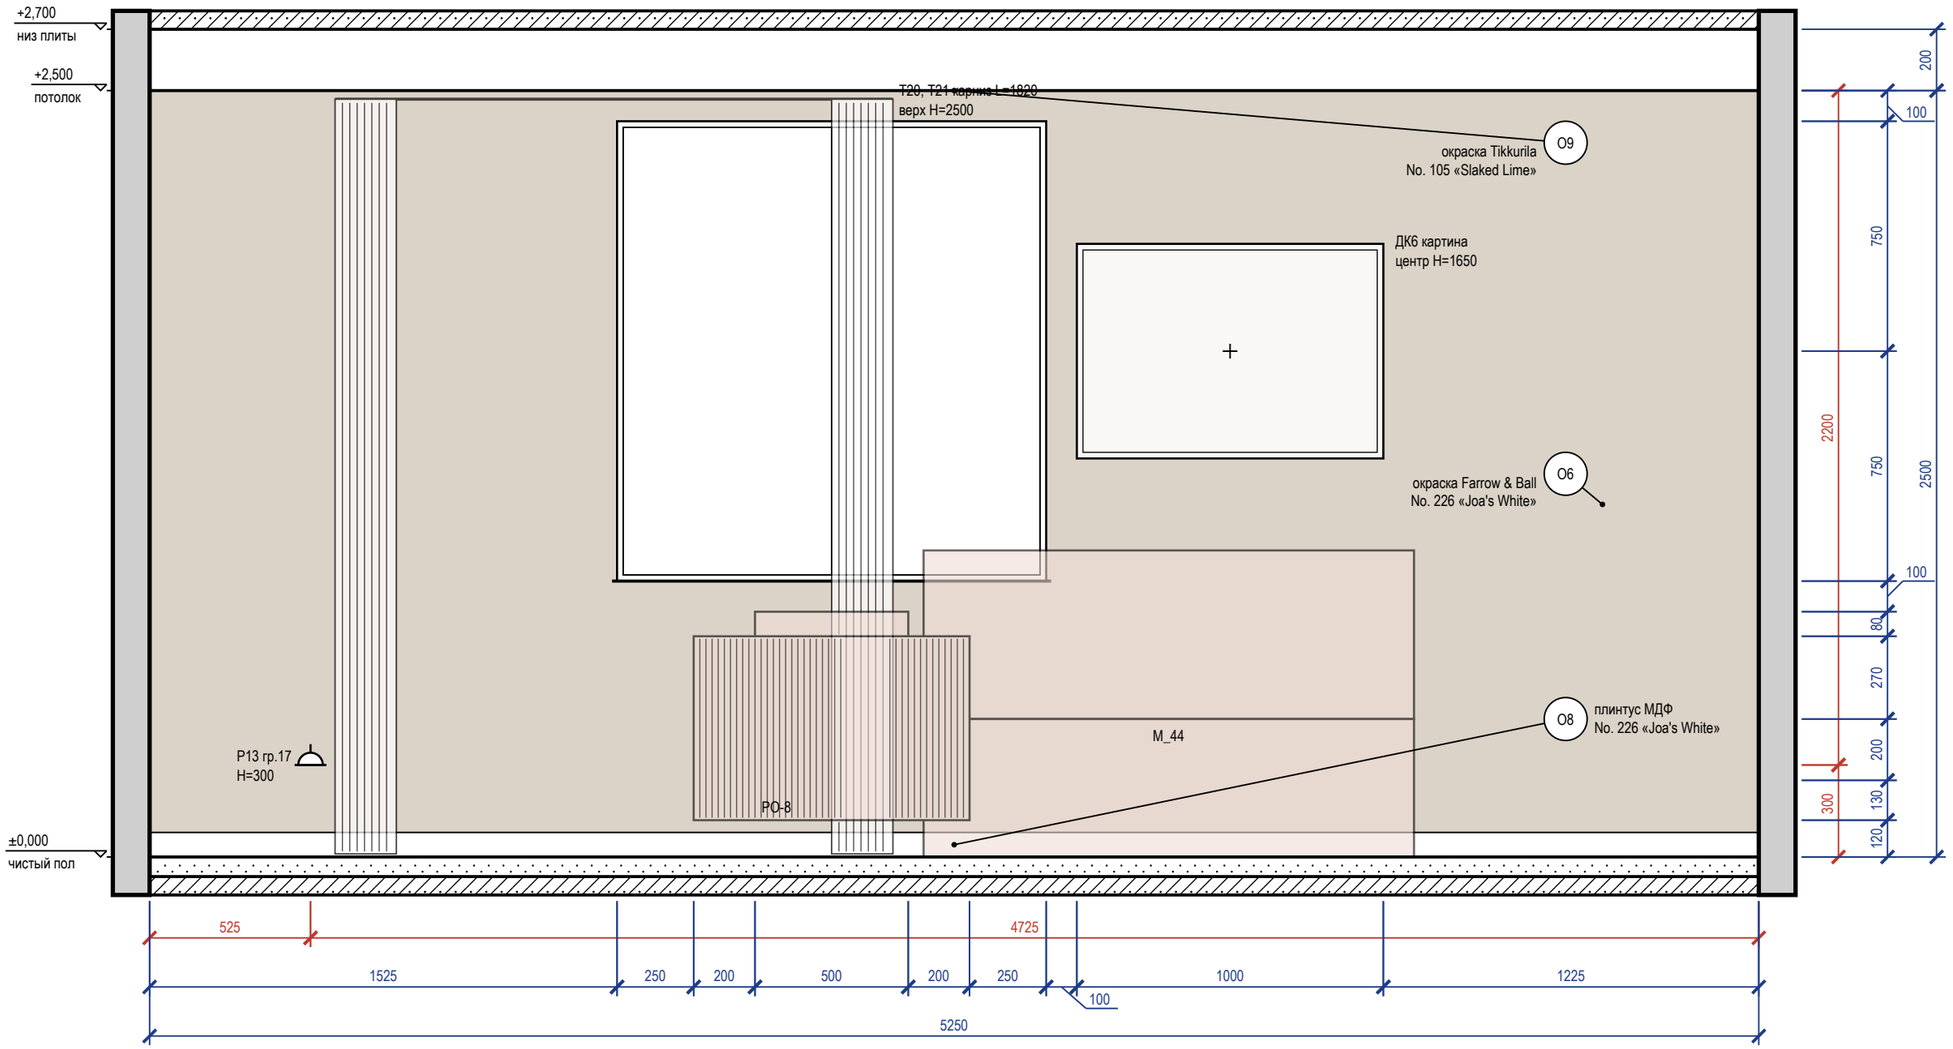


### Схема развёрток (М 1:100)

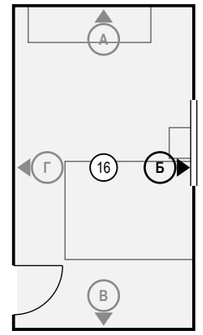


### Ведомость отделки (на листе)

| Марка | Поверхность | Материал, изделие | Цвет, код | Кол. |
|---|---|---|---|---|
| О6 | стены | окраска, Farrow & Ball Modern Emulsion, матовая, подготовка Q3 | Farrow & Ball No. 226 «Joa's White» | 11 м² |
| О8 | плинтус | плинтус МДФ, h 80 мм, аналог: плинтус МДФ под покраску 80×16 | Farrow & Ball No. 226 «Joa's White» | 5,3 м |
| О9 | потолок | окраска, Tikkurila Anti-Reflex 2, глубокоматовая, подготовка Q3 | Little Greene No. 105 «Slaked Lime» | 15,5 м² |

Визуализация этой стены

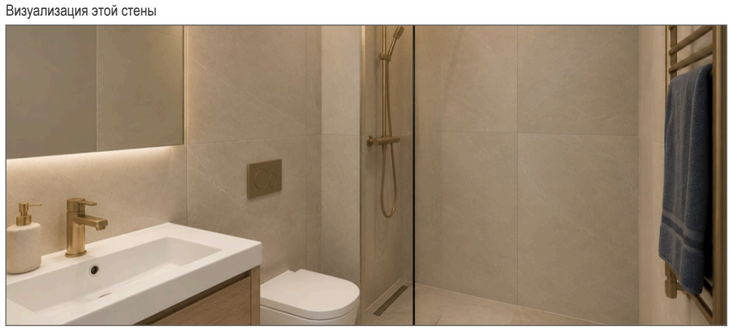

### Примечания

1. Размеры — в мм от чистовых поверхностей стен; условные обозначения и общие указания — лист 2.
2. Картины и зеркала крепить к основанию по паспорту изделия (закладные и анкеры — в перечне скрытых работ); крест — ось центра предмета.
3. Карнизы (шины) — по ведомости текстиля декоратора; длина L и верх H — по развёртке, крепление — до окраски потолка.
4. Потолок на развёртках — по нижнему уровню У1; другие уровни потолка помещения: У2 +2,600.
5. Линии узора (швы плитки, складки штор, рёбра радиаторов) прерываются у знаков и выносок — просвет между линиями не менее 0,7 мм.

| | Лист | № док. | Подпись | Дата |
|---|---|---|---|---|
| Дизайнер | Кырлан А.С. | | | 19.10.26 |

Проект: Дом 331 м²

Развёртка стены Б. Спальня 2 (пом. 16)

| Стадия | Лист | Листов |
|---|---|---|
| П | 119 | 156 |

выпуск 18.10.2026 № 8cd922c868 · стр. 119 из 156

Правка к этому листу

## Развёртка стены В

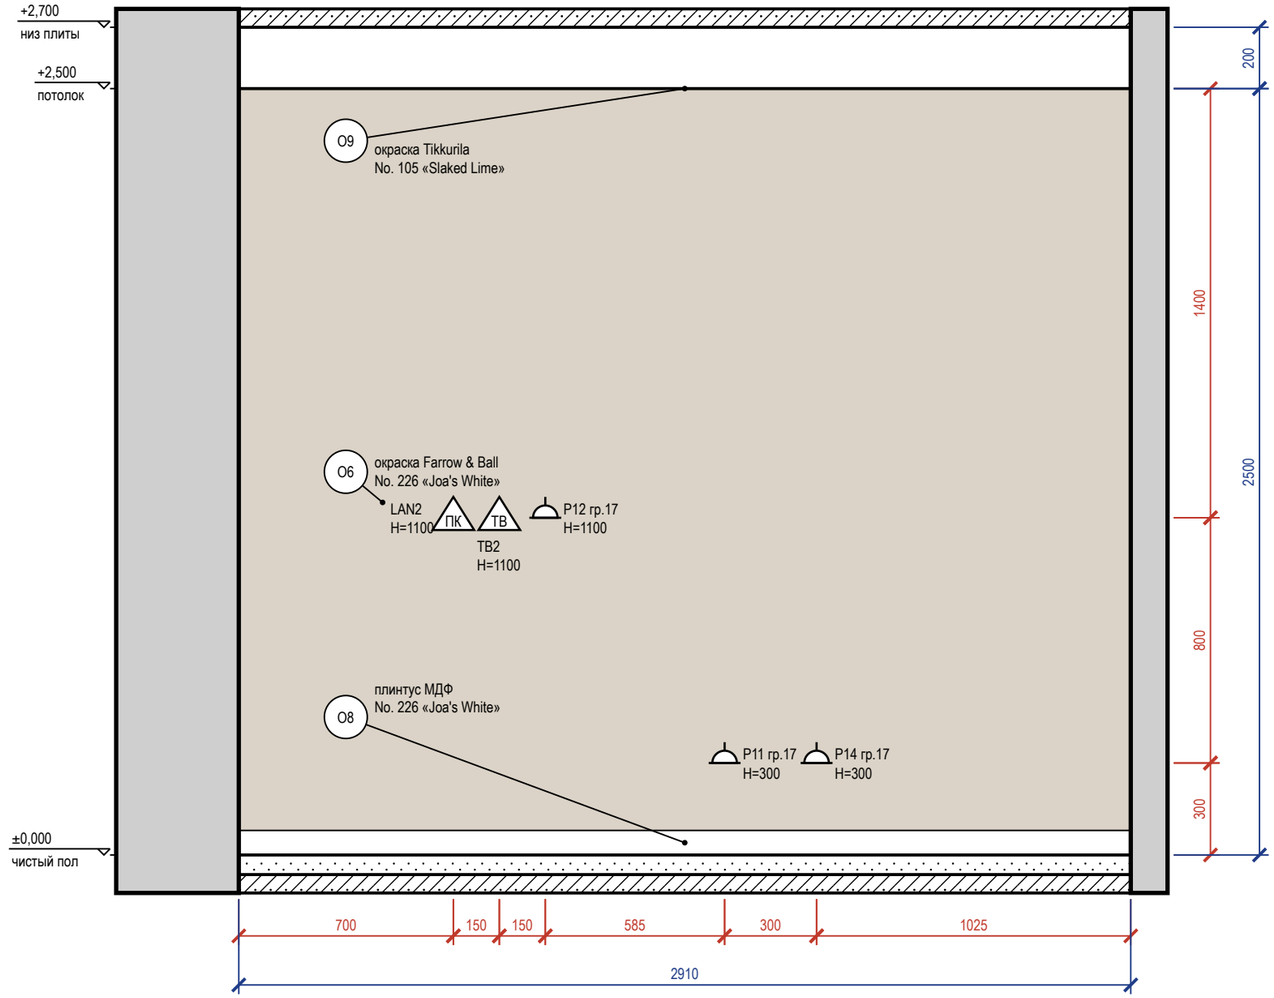


## Схема развёрток (М 1:100)

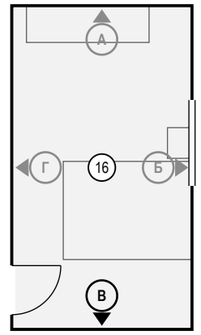


## Ведомость отделки (на листе)

| Марка | Поверхность | Материал, изделие | Цвет, код | Кол. |
|---|---|---|---|---|
| О6 | стены | окраска, Farrow & Ball Modern Emulsion, матовая, подготовка Q3 | Farrow & Ball No. 226 «Joa's White» | 7,3 м² |
| О8 | плинтус | плинтус МДФ, h 80 мм, аналог: плинтус МДФ под покраску 80×16 | Farrow & Ball No. 226 «Joa's White» | 2,9 м |
| О9 | потолок | окраска, Tikkurila Anti-Reflex 2, глубокоматовая, подготовка Q3 | Little Greene No. 105 «Slaked Lime» | 15,5 м² |

## Примечания

1. Размеры — в мм от чистовых поверхностей стен; условные обозначения и общие указания — лист 2.
2. Потолок на развёртках — по нижнему уровню У1; другие уровни потолка помещения: У2 +2,600.

| | | | | | |
|---|---|---|---|---|---|
| | | | | | Проект: Дом 331 м² |
| | Лист | № док. | Подпись | Дата | Развёртка стены В. Спальня 2 (пом. 16) |
| Дизайнер | Кырлан А.С. | | | 19.10.26 | |

| Стадия | Лист | Листов |
|---|---|---|
| П | 120 | 156 |

выпуск 18.10.2026 № 8cd922c868 · стр. 120 из 156

Правка к этому листу

## Развёртка стены Г

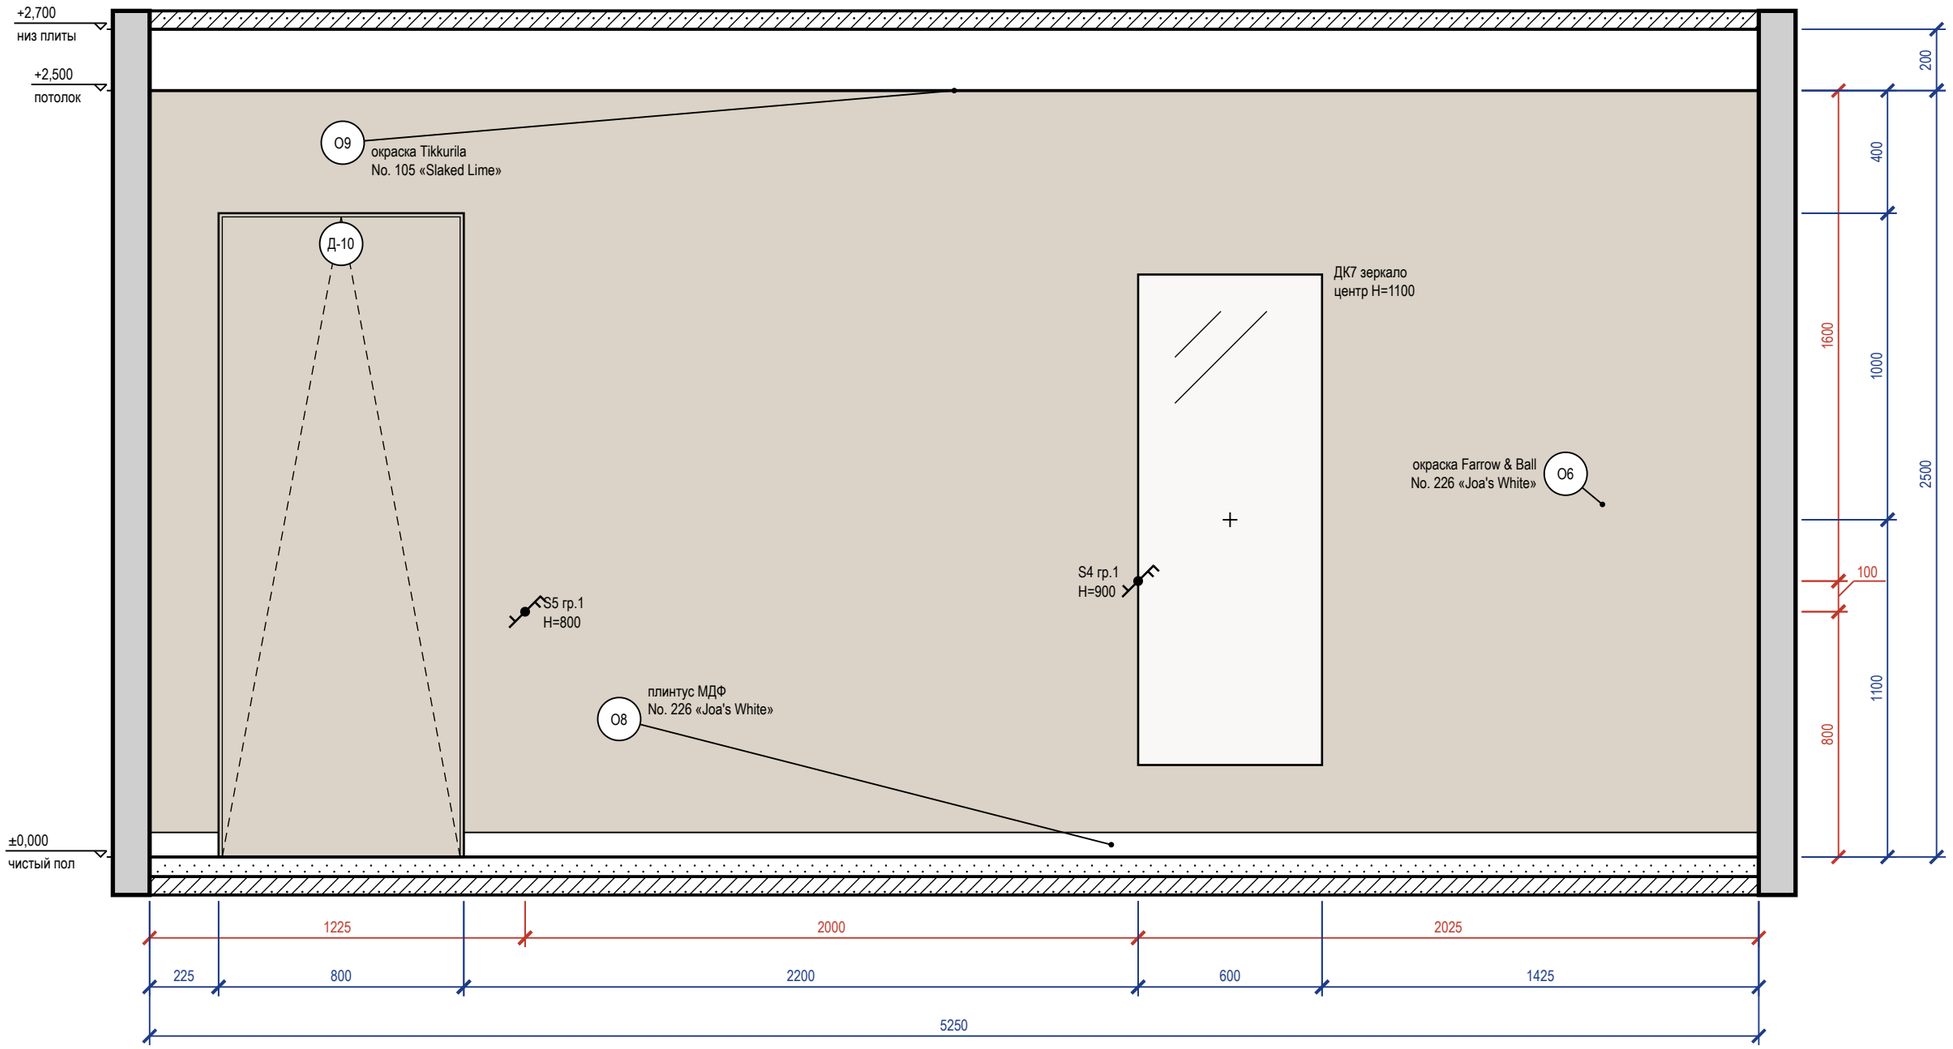


### Схема развёрток (М 1:100)

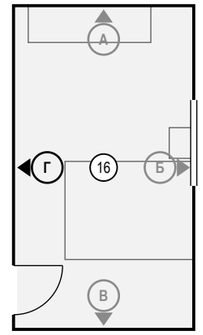


### Ведомость отделки (на листе)

| Марка | Поверхность | Материал, изделие | Цвет, код | Кол. |
|---|---|---|---|---|
| О6 | стены | окраска, Farrow & Ball Modern Emulsion, матовая, подготовка Q3 | Farrow & Ball No. 226 «Joa's White» | 11,4 м² |
| О8 | плинтус | плинтус МДФ, h 80 мм, аналог: плинтус МДФ под покраску 80×16 | Farrow & Ball No. 226 «Joa's White» | 4,5 м |
| О9 | потолок | окраска, Tikkurila Anti-Reflex 2, глубокоматовая, подготовка Q3 | Little Greene No. 105 «Slaked Lime» | 15,5 м² |

### Примечания

1. Размеры — в мм от чистовых поверхностей стен; условные обозначения и общие указания — лист 2.
2. Картины и зеркала крепить к основанию по паспорту изделия (закладные и анкеры — в перечне скрытых работ); крест — ось центра предмета.
3. Двери скрытого монтажа — полотно в плоскости стены, отделка стены по полотну, плинтус прерывается у короба (узел — на листе узлов).
4. Потолок на развёртках — по нижнему уровню У1; другие уровни потолка помещения: У2 +2,600.

| | | | | | |
|---|---|---|---|---|---|
| | | | | | Проект: Дом 331 м² |
| | Лист | № док. | Подпись | Дата | Развёртка стены Г. Спальня 2 (пом. 16) |
| Дизайнер | Кырлан А.С. | | | 19.10.26 | |

| Стадия | Лист | Листов |
|---|---|---|
| П | 121 | 156 |

выпуск 18.10.2026 № 8cd922c868 · стр. 121 из 156

Правка к этому листу

| | | | | | | |
|---|---|---|---|---|---|---|
| | | | | | Проект: Дом 331 м² | |
| | Лист | № док. | Подпись | Дата | | |
| Дизайнер | Кырлан А.С. | | | 19.10.26 | Визуализация: Холл мансарды | Стадия / Лист / Листов |
| | | | | | | П / 122 / 156 |

выпуск 18.10.2026 № 8cd922c868 · стр. 122 из 156

Правка к этому листу

## Развёртка стены А

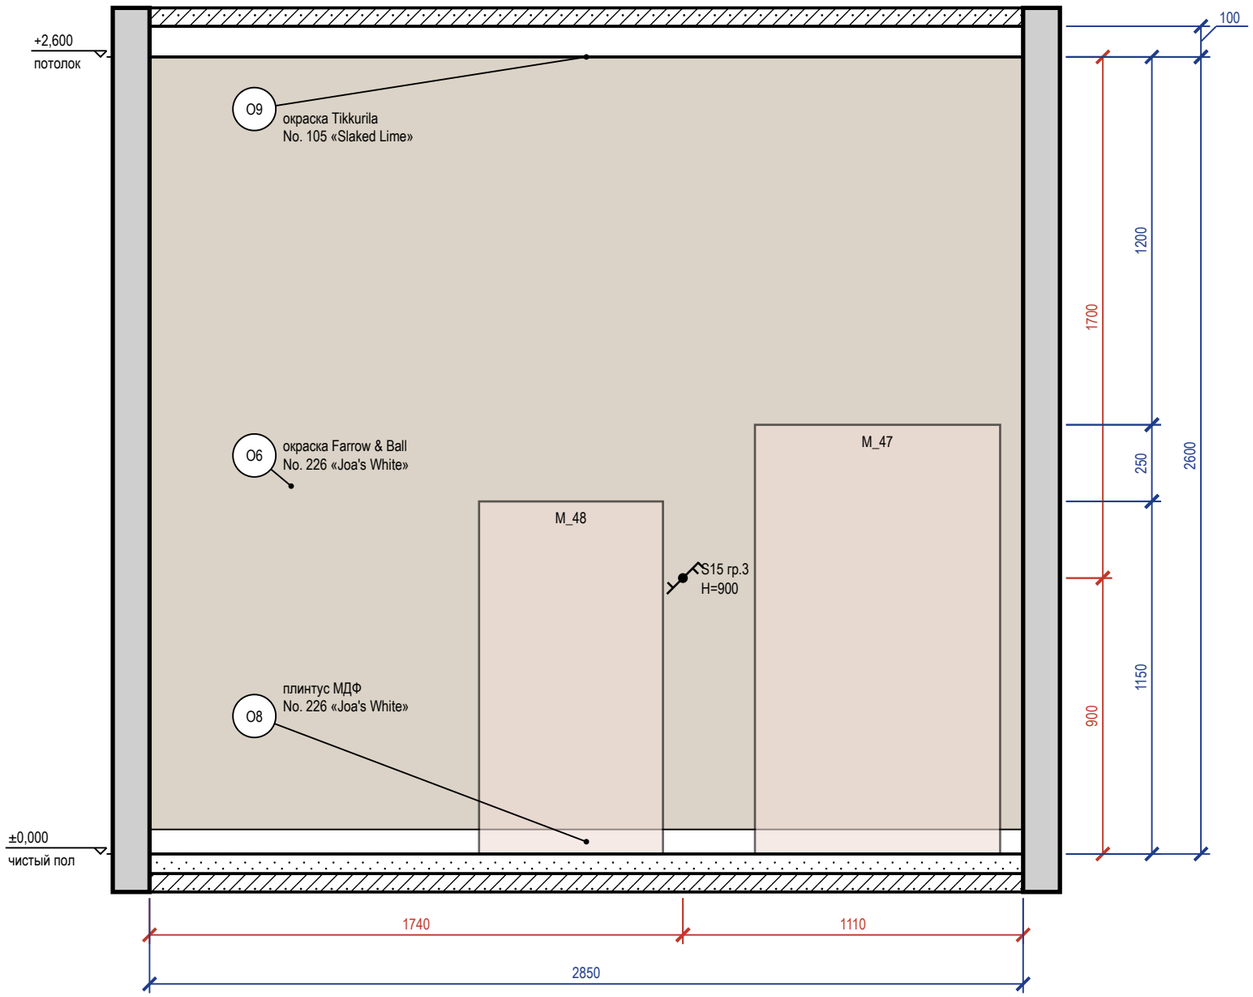


## Схема развёрток (М 1:100)

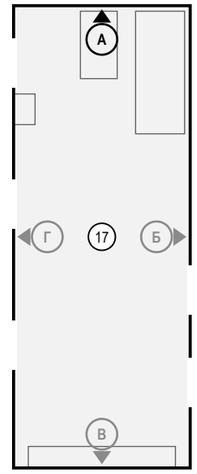


## Ведомость отделки (на листе)

| Марка | Поверхность | Материал, изделие | Цвет, код | Кол. |
|---|---|---|---|---|
| О6 | стены | окраска, Farrow & Ball Modern Emulsion, матовая, подготовка Q3 | Farrow & Ball No. 226 «Joa's White» | 7,4 м² |
| О8 | плинтус | плинтус МДФ, h 80 мм, аналог: плинтус МДФ под покраску 80×16 | Farrow & Ball No. 226 «Joa's White» | 2,9 м |
| О9 | потолок | окраска, Tikkurila Anti-Reflex 2, глубокоматовая, подготовка Q3 | Little Greene No. 105 «Slaked Lime» | 21,7 м² |

## Примечания

1. Размеры — в мм от чистовых поверхностей стен; условные обозначения и общие указания — лист 2.

| | | | | | |
|---|---|---|---|---|---|
| | | | | | Проект: Дом 331 м² |
| | Лист | № док. | Подпись | Дата | Развёртка стены А. Холл мансарды (пом. 17) |
| Дизайнер | Кырлан А.С. | | | 19.10.26 | |

| Стадия | Лист | Листов |
|---|---|---|
| П | 123 | 156 |

выпуск 18.10.2026 № 8cd922c868 · стр. 123 из 156

Правка к этому листу

## Развёртка стены Б

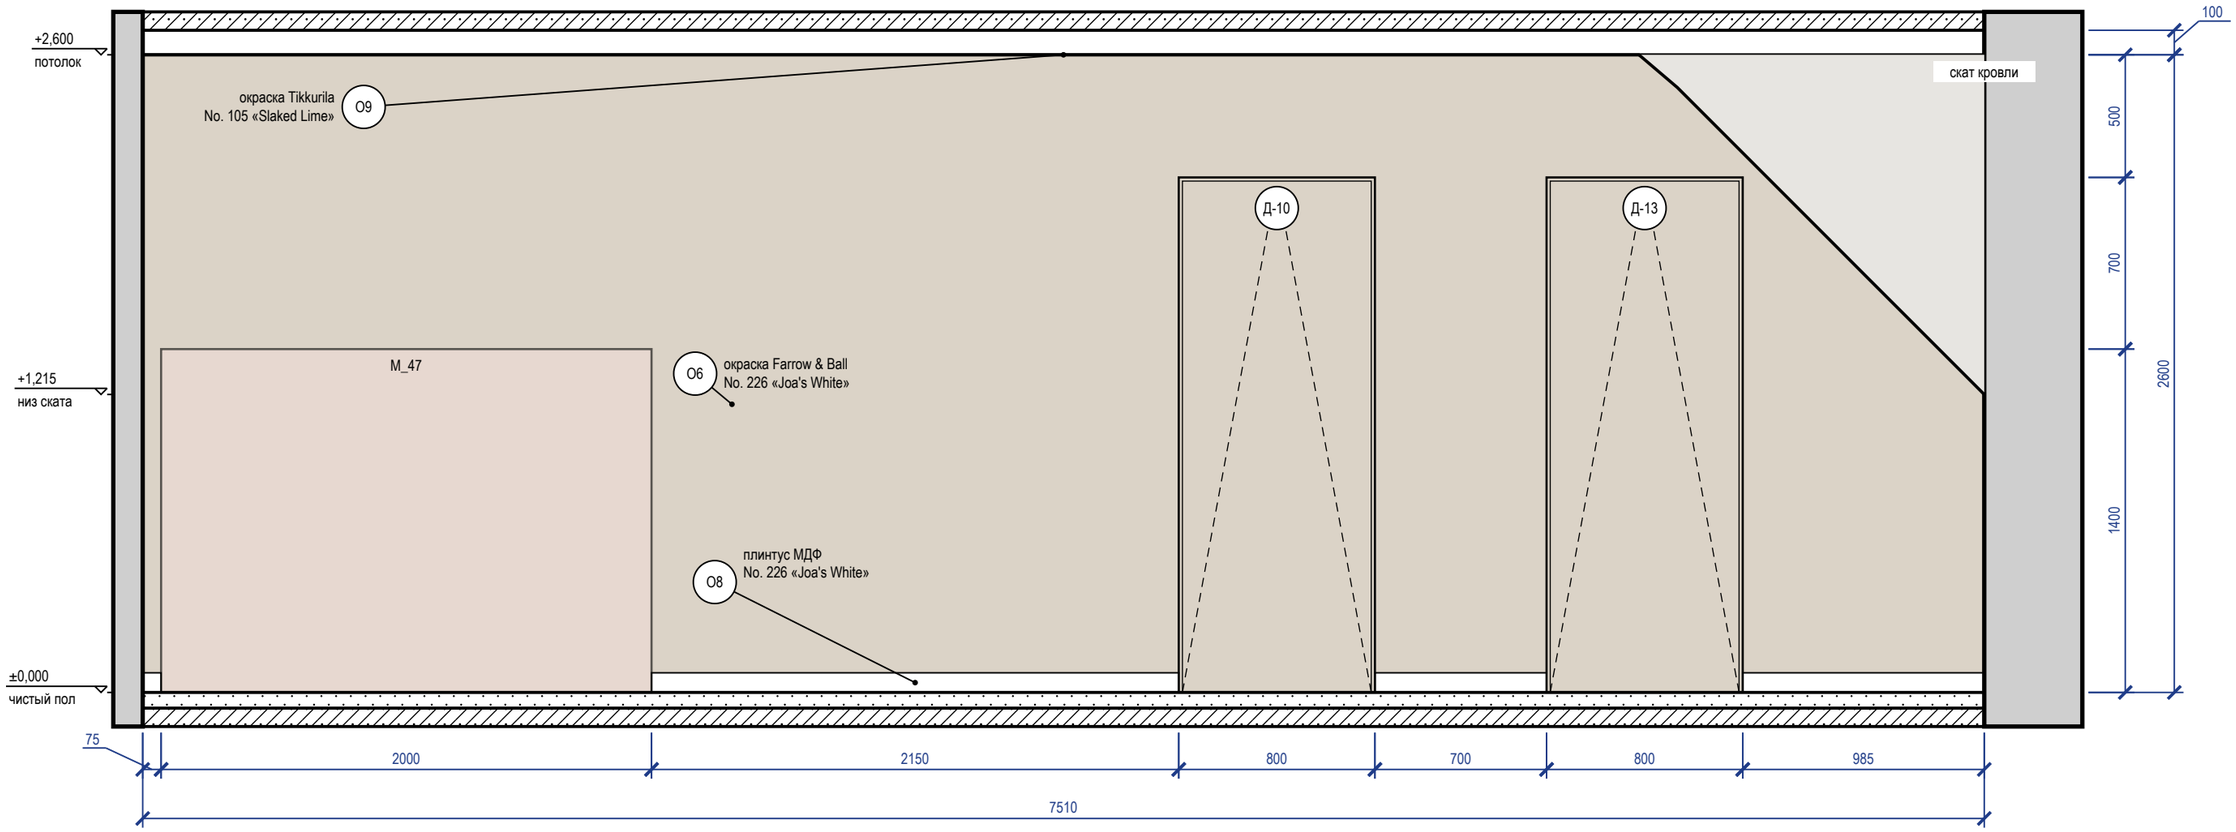


### Схема развёрток (М 1:100)

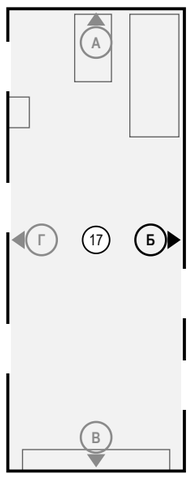


### Ведомость отделки (на листе)

| Марка | Поверхность | Материал, изделие | Цвет, код | Кол. |
|---|---|---|---|---|
| О6 | стены | окраска, Farrow & Ball Modern Emulsion, матовая, подготовка Q3 | Farrow & Ball No. 226 «Joa's White» | 16,2 м² |
| О8 | плинтус | плинтус МДФ, h 80 мм, аналог: плинтус МДФ под покраску 80×16 | Farrow & Ball No. 226 «Joa's White» | 3,9 м |
| О9 | потолок | окраска, Tikkurila Anti-Reflex 2, глубокоматовая, подготовка Q3 | Little Greene No. 105 «Slaked Lime» | 21,7 м² |

### Примечания

1. Размеры — в мм от чистовых поверхностей стен; условные обозначения и общие указания — лист 2.
2. Двери скрытого монтажа — полотно в плоскости стены, отделка стены по полотну, плинтус прерывается у короба (узел — на листе узлов).

| | | | | | |
|---|---|---|---|---|---|
| | | | | | Проект: Дом 331 м² |
| | Лист | № док. | Подпись | Дата | Развёртка стены Б. Холл мансарды (пом. 17) |
| Дизайнер | Кырлан А.С. | | | 19.10.26 | |

| Стадия | Лист | Листов |
|---|---|---|
| П | 124 | 156 |

выпуск 18.10.2026 · 8cd922c868 · стр. 124 из 156

Правка к этому листу

## Развёртка стены В

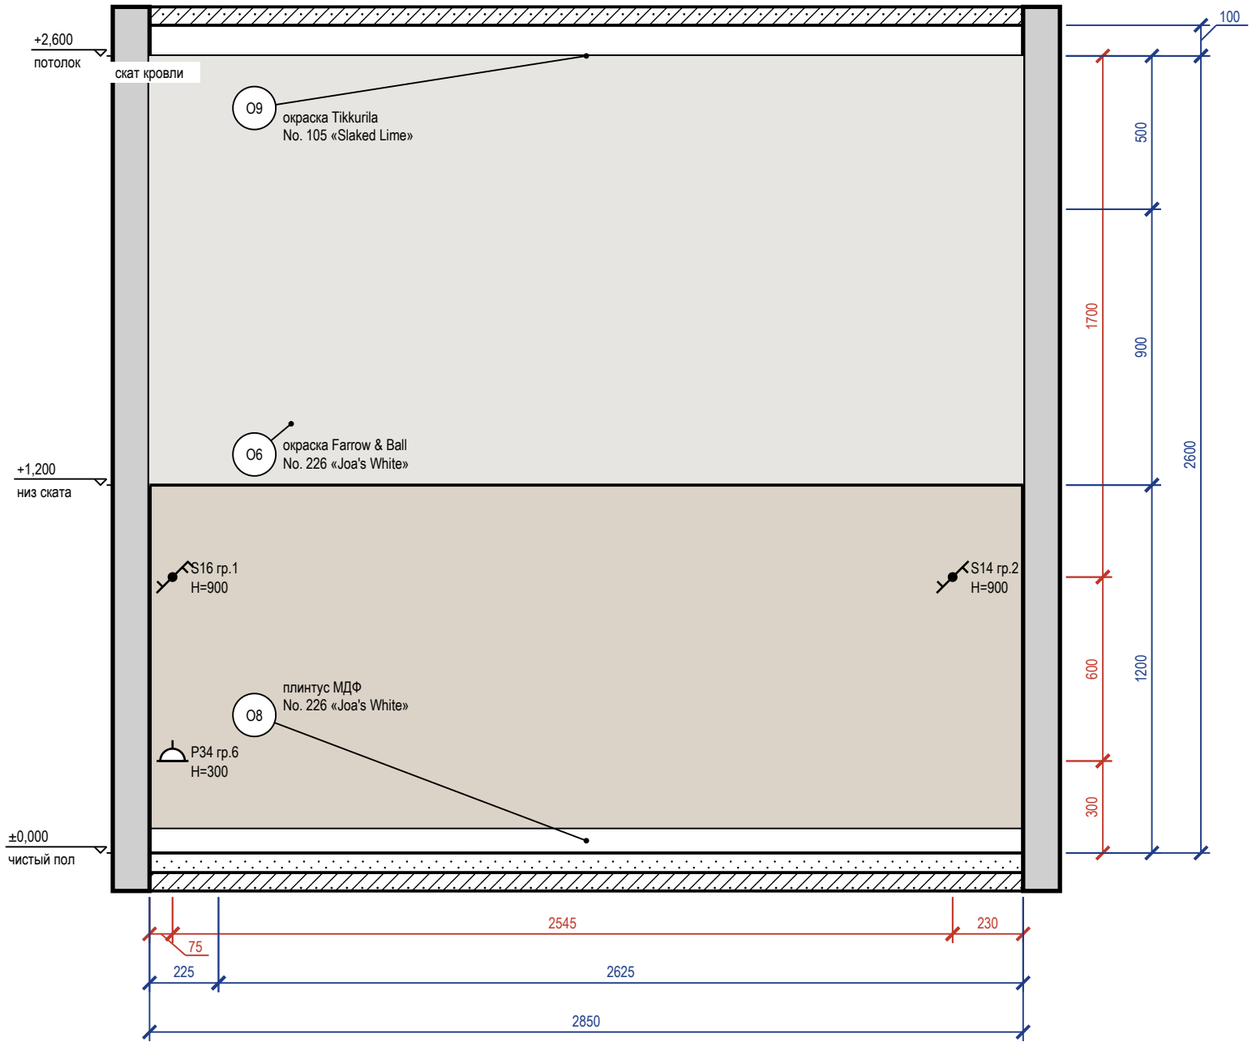


## Схема развёрток (М 1:100)

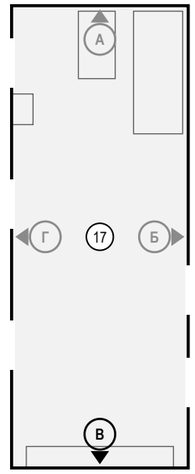


## Ведомость отделки (на листе)

| Марка | Поверхность | Материал, изделие | Цвет, код | Кол. |
|---|---|---|---|---|
| О6 | стены | окраска, Farrow & Ball Modern Emulsion, матовая, подготовка Q3 | Farrow & Ball No. 226 «Joa's White» | 7,4 м² |
| О8 | плинтус | плинтус МДФ, h 80 мм, аналог: плинтус МДФ под покраску 80×16 | Farrow & Ball No. 226 «Joa's White» | 2,9 м |
| О9 | потолок | окраска, Tikkurila Anti-Reflex 2, глубокоматовая, подготовка Q3 | Little Greene No. 105 «Slaked Lime» | 21,7 м² |

Визуализация этой стены — лист 122

### Примечания

1. Размеры — в мм от чистовых поверхностей стен; условные обозначения и общие указания — лист 2.
2. Схема мебели, приборов и декора не является технической документацией для производства мебели; габариты — по паспортам изделий.

| | | | | | |
|---|---|---|---|---|---|
| | | | | | Проект: Дом 331 м² |
| | Лист | № док. | Подпись | Дата | Развёртка стены В. Холл мансарды (пом. 17) |
| Дизайнер | Кырлан А.С. | | | 19.10.26 | |

| Стадия | Лист | Листов |
|---|---|---|
| П | 125 | 156 |

выпуск 18.10.2026 № 8cd922c868 · стр. 125 из 156

Правка к этому листу

## Развёртка стены Г

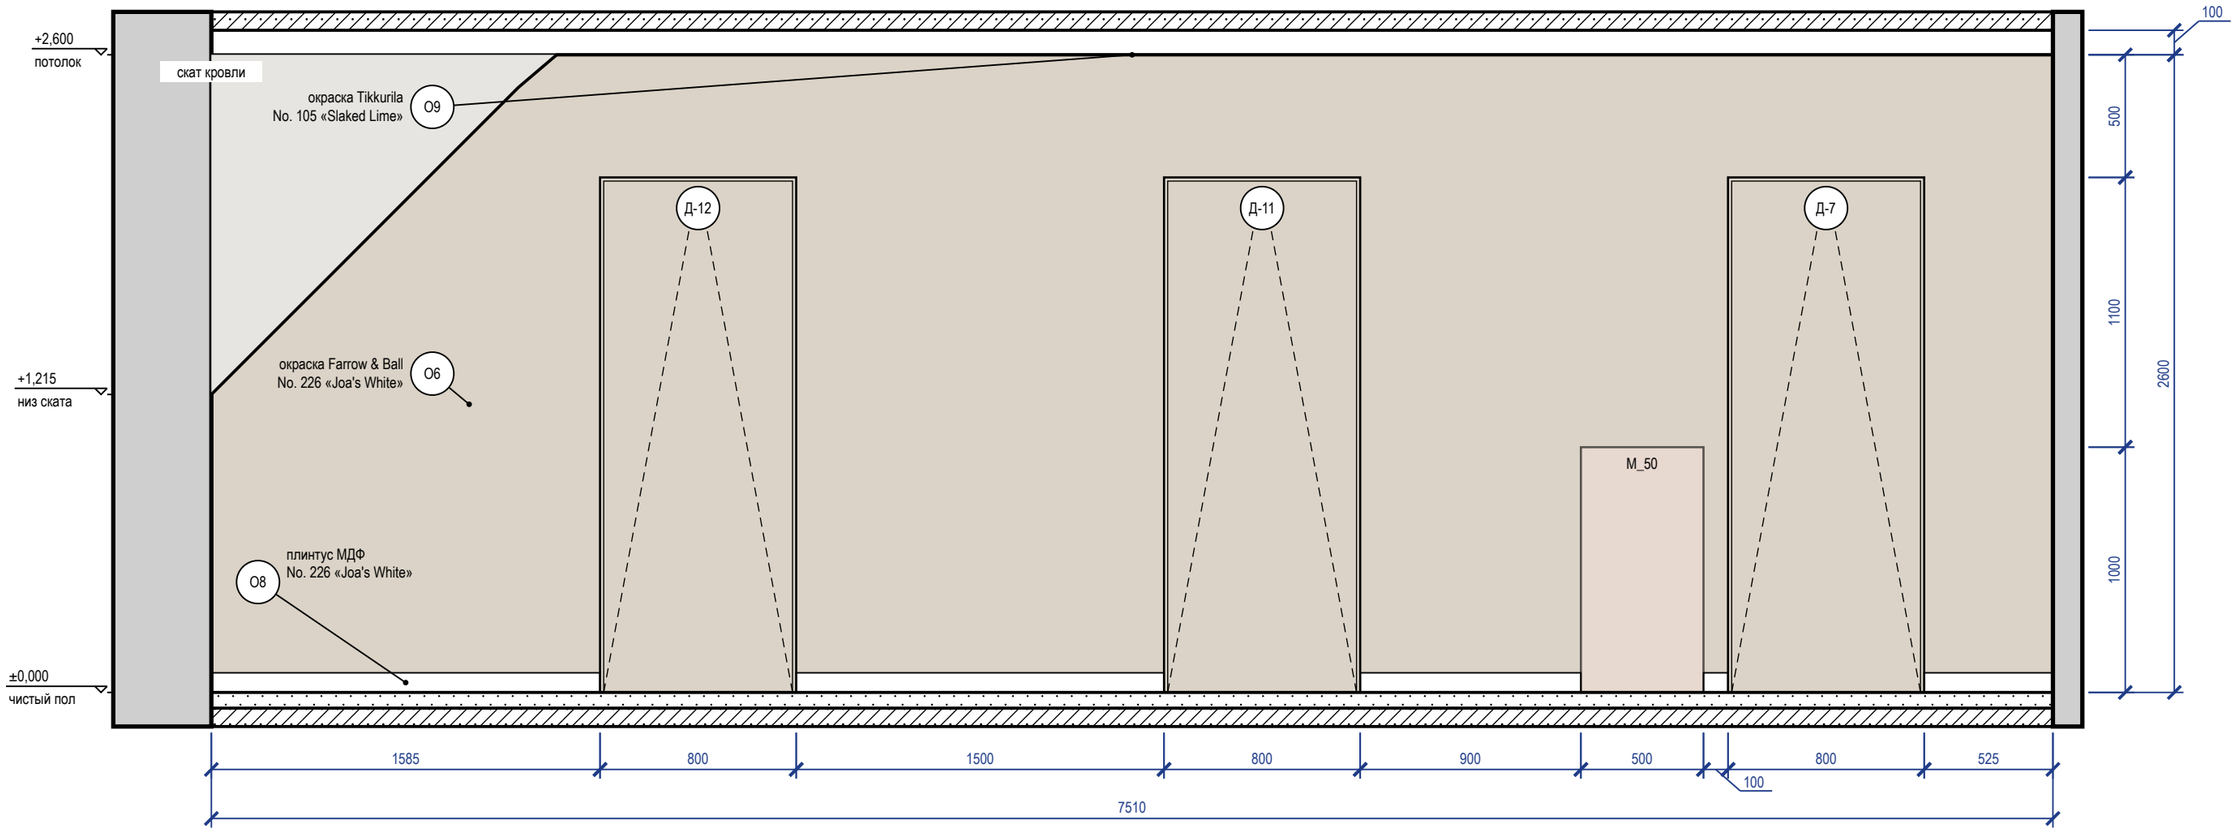


### Схема развёрток (М 1:100)

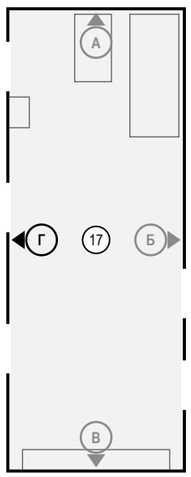


### Ведомость отделки (на листе)

| Марка | Поверхность | Материал, изделие | Цвет, код | Кол. |
|---|---|---|---|---|
| О6 | стены | окраска, Farrow & Ball Modern Emulsion, матовая, подготовка Q3 | Farrow & Ball No. 226 «Joa's White» | 14,5 м² |
| О8 | плинтус | плинтус МДФ, h 80 мм, аналог: плинтус МДФ под покраску 80×16 | Farrow & Ball No. 226 «Joa's White» | 4,6 м |
| О9 | потолок | окраска, Tikkurila Anti-Reflex 2, глубокоматовая, подготовка Q3 | Little Greene No. 105 «Slaked Lime» | 21,7 м² |

### Примечания

1. Размеры — в мм от чистовых поверхностей стен; условные обозначения и общие указания — лист 2.
2. Двери скрытого монтажа — полотно в плоскости стены, отделка стены по полотну, плинтус прерывается у короба (узел — на листе узлов).

| | | | | | |
|---|---|---|---|---|---|
| | | | | | Проект: Дом 331 м² |
| | Лист | № док. | Подпись | Дата | Развёртка стены Г. Холл мансарды (пом. 17) |
| Дизайнер | Кырлан А.С. | | | 19.10.26 | |

| Стадия | Лист | Листов |
|---|---|---|
| П | 126 | 156 |

выпуск 18.10.2026 № 8cd922c868 · стр. 126 из 156

Правка к этому листу

| | | | | | | |
|---|---|---|---|---|---|---|
| | | | | | Проект: Дом 331 м² | |
| | Лист | № док. | Подпись | Дата | | |
| Дизайнер | Кырлан А.С. | | | 19.10.26 | Визуализация: Спальня 3 | Стадия / Лист / Листов |
| | | | | | | П / 127 / 156 |

выпуск 18.10.2026 № 8cd922c868 · стр. 127 из 156

Правка к этому листу

| | | | | | | |
|---|---|---|---|---|---|---|
| | | | | | Проект: Дом 331 м² | |
| | Лист | № док. | Подпись | Дата | Визуализация: Спальня 3 | Стадия / Лист / Листов |
| Дизайнер | Кырлан А.С. | | | 19.10.26 | | П / 128 / 156 |

выпуск 18.10.2026 № 8cd922c868 · стр. 128 из 156

Правка к этому листу

## Развёртка стены А

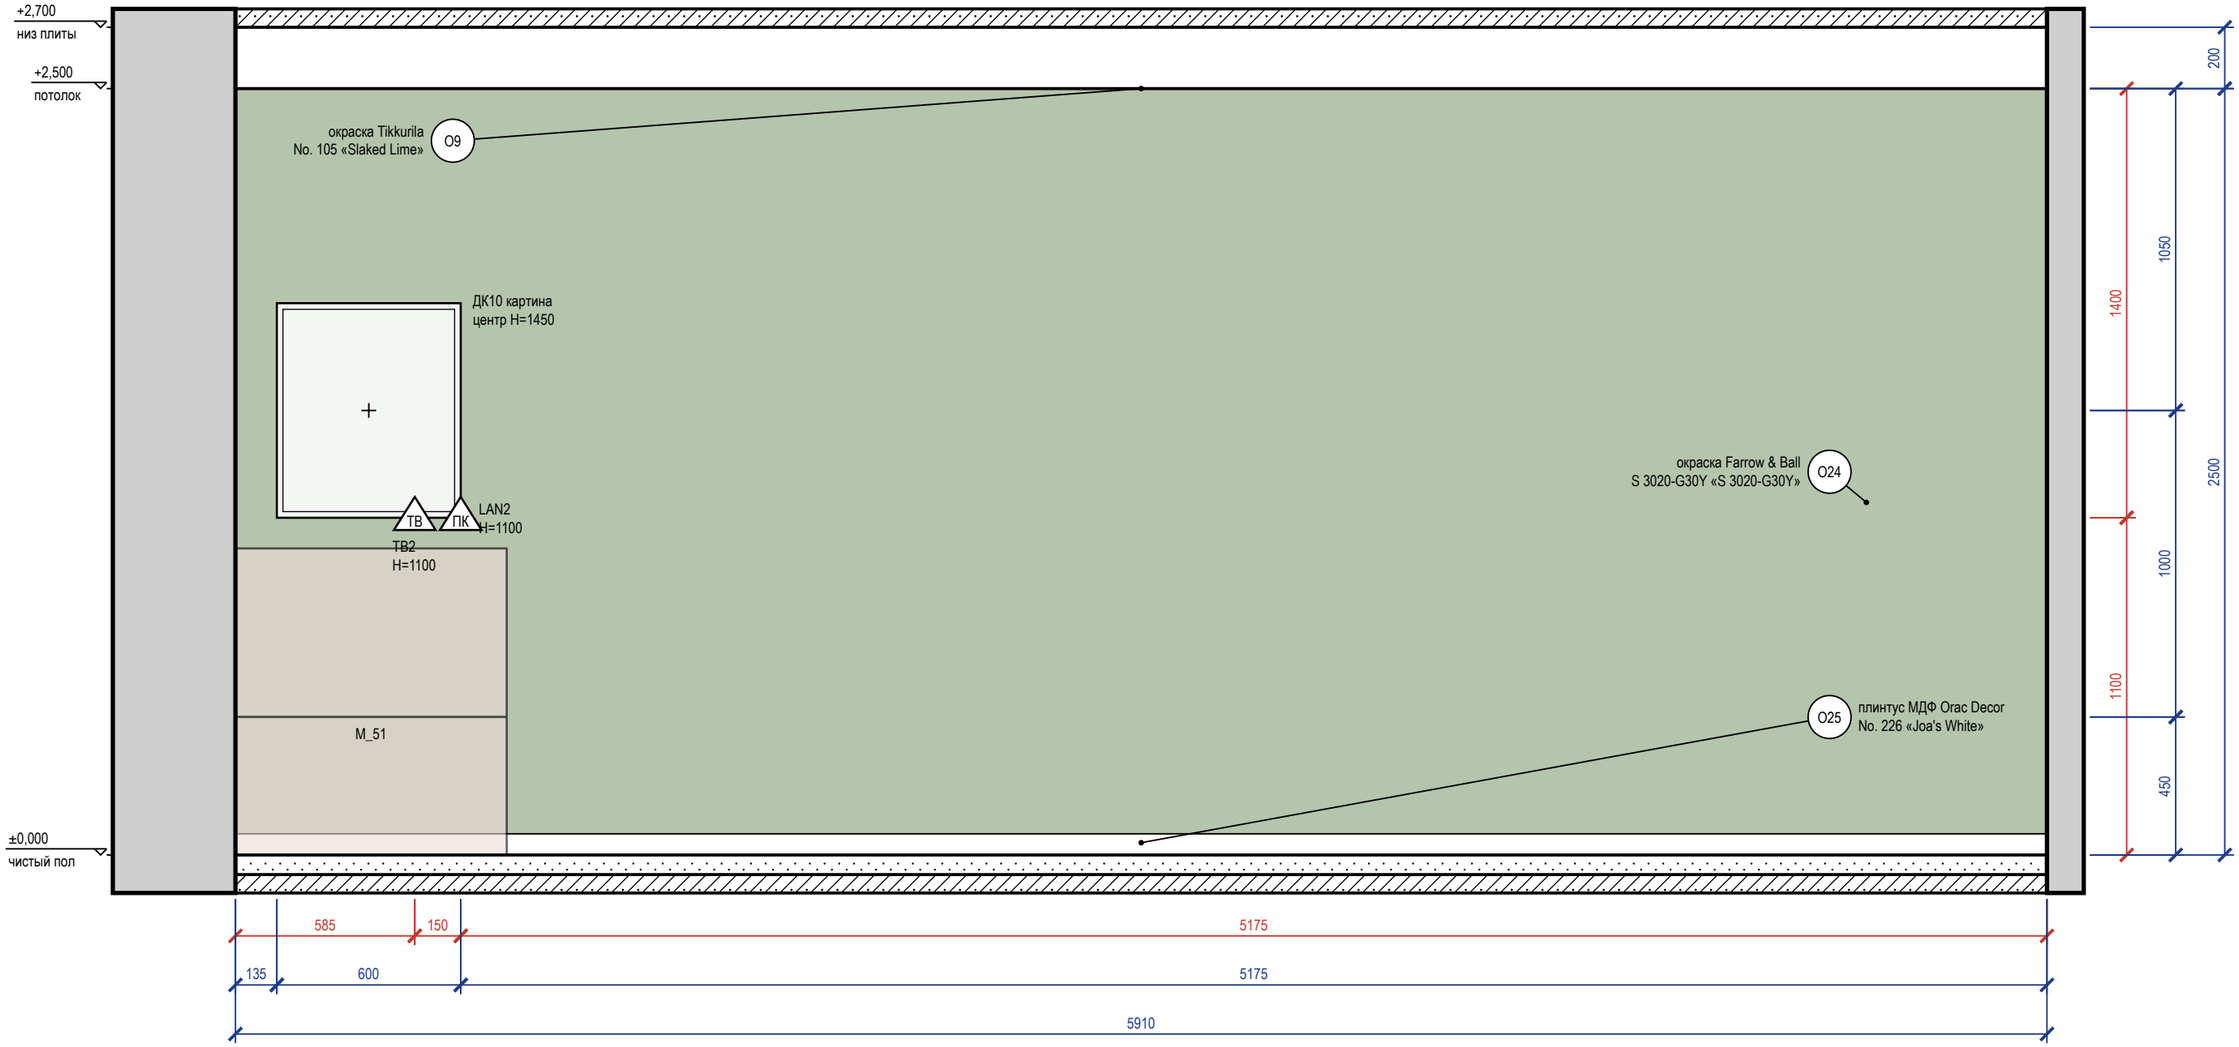


### Схема развёрток (М 1:100)

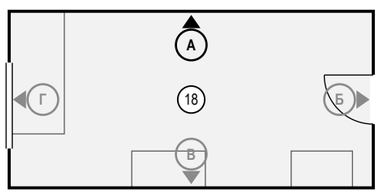


### Ведомость отделки (на листе)

| Марка | Поверхность | Материал, изделие | Цвет, код | Кол. |
|---|---|---|---|---|
| O9 | потолок | окраска, Tikkurila Anti-Reflex 2, глубокоматовая, подготовка Q3 | Little Greene No. 105 «Slaked Lime» | 17,1 м² |
| O24 | акцентная стена | окраска, Farrow & Ball Modern Emulsion, матовая, подготовка Q3 | NCS S 3020-G30Y «S 3020-G30Y» | 14,8 м² |
| O25 | плинтус | плинтус МДФ, Orac Decor Contour (Luxxus), h 69 мм, SX165 | Farrow & Ball No. 226 «Joa's White» | 5,9 м |

Визуализация этой стены

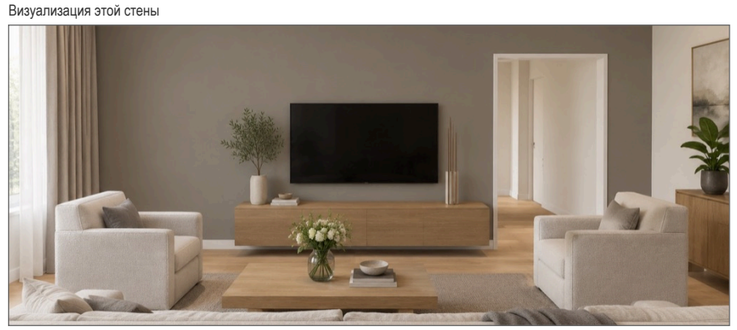

### Примечания

1. Размеры — в мм от чистовых поверхностей стен; условные обозначения и общие указания — лист 2.
2. Картины и зеркала крепить к основанию по паспорту изделия (закладные и анкеры — в перечне скрытых работ); крест — ось центра предмета.
3. Потолок на развёртках — по нижнему уровню У1; другие уровни потолка помещения: У2 +2,600.

| | | | | | |
|---|---|---|---|---|---|
| | | | | | Проект: Дом 331 м² |
| | Лист | № док. | Подпись | Дата | |
| Дизайнер | Кырлан А.С. | | | 19.10.26 | Развёртка стены А. Спальня 3 (пом. 18) |

| Стадия | Лист | Листов |
|---|---|---|
| П | 129 | 156 |

выпуск 18.10.2026 № 8cd922c868 · стр. 129 из 156

Правка к этому листу

## Развёртка стены Б

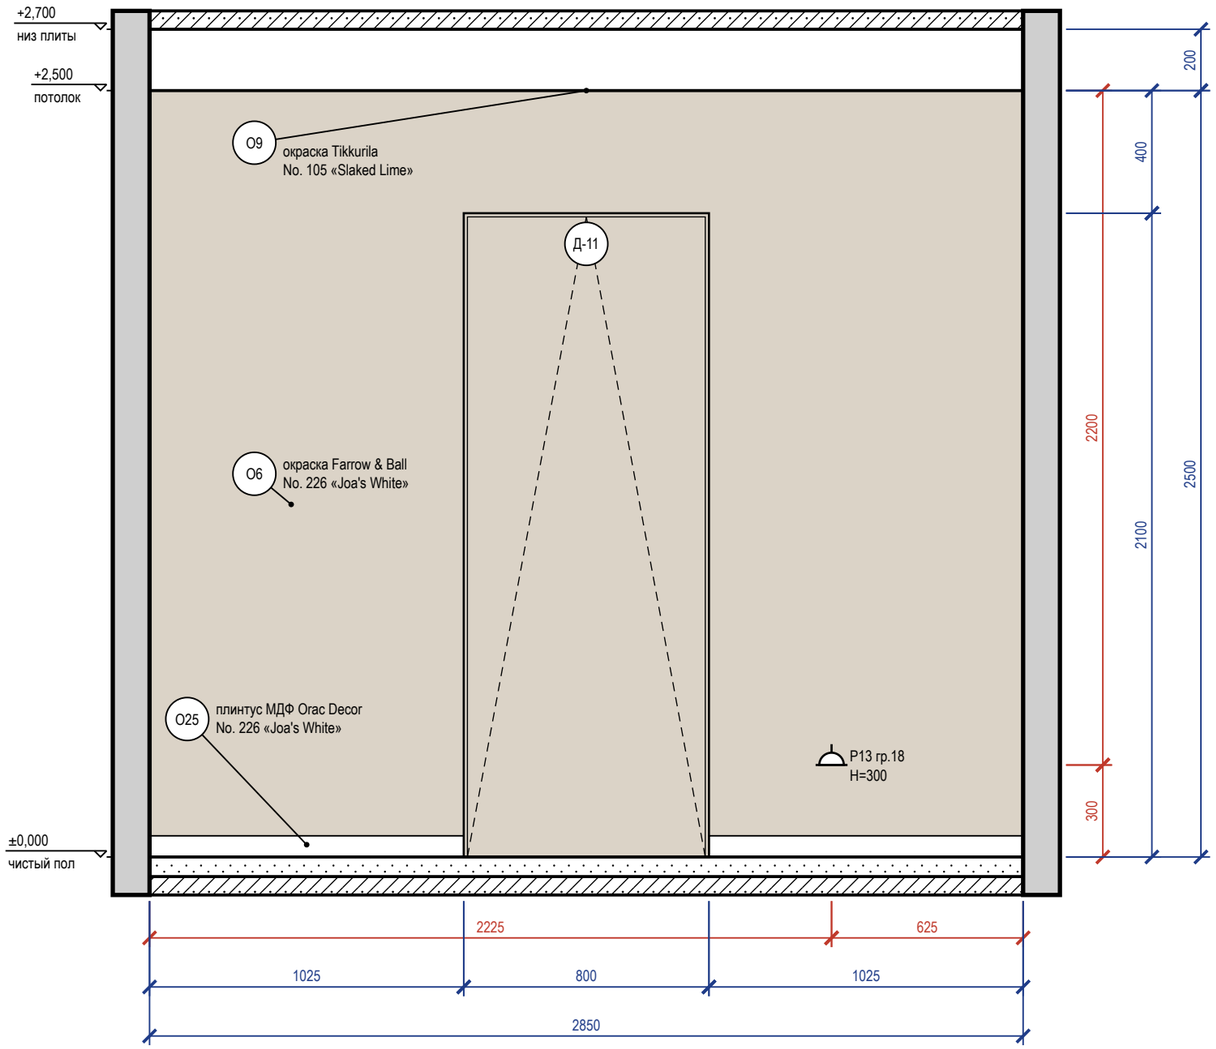


## Схема развёрток (М 1:100)

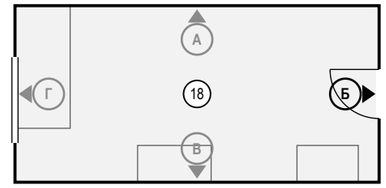


## Ведомость отделки (на листе)

| Марка | Поверхность | Материал, изделие | Цвет, код | Кол. |
|---|---|---|---|---|
| О6 | стены | окраска, Farrow & Ball Modern Emulsion, матовая, подготовка Q3 | Farrow & Ball No. 226 «Joa's White» | 5,4 м² |
| О9 | потолок | окраска, Tikkurila Anti-Reflex 2, глубокоматовая, подготовка Q3 | Little Greene No. 105 «Slaked Lime» | 17,1 м² |
| О25 | плинтус | плинтус МДФ, Orac Decor Contour (Luxxus), h 69 мм, SX165 | Farrow & Ball No. 226 «Joa's White» | 2 м |

## Примечания

1. Размеры — в мм от чистовых поверхностей стен; условные обозначения и общие указания — лист 2.
2. Двери скрытого монтажа — полотно в плоскости стены, отделка стены по полотну, плинтус прерывается у короба (узел — на листе узлов).
3. Потолок на развёртках — по нижнему уровню У1; другие уровни потолка помещения: У2 +2,600.

| | | | | | |
|---|---|---|---|---|---|
| | | | | | Проект: Дом 331 м² |
| | Лист | № док. | Подпись | Дата | Развёртка стены Б. Спальня 3 (пом. 18) |
| Дизайнер | Кырлан А.С. | | | 19.10.26 | |

| Стадия | Лист | Листов |
|---|---|---|
| П | 130 | 156 |

выпуск 18.10.2026 № 8cd922c868 · стр. 130 из 156

Правка к этому листу

## Развёртка стены В

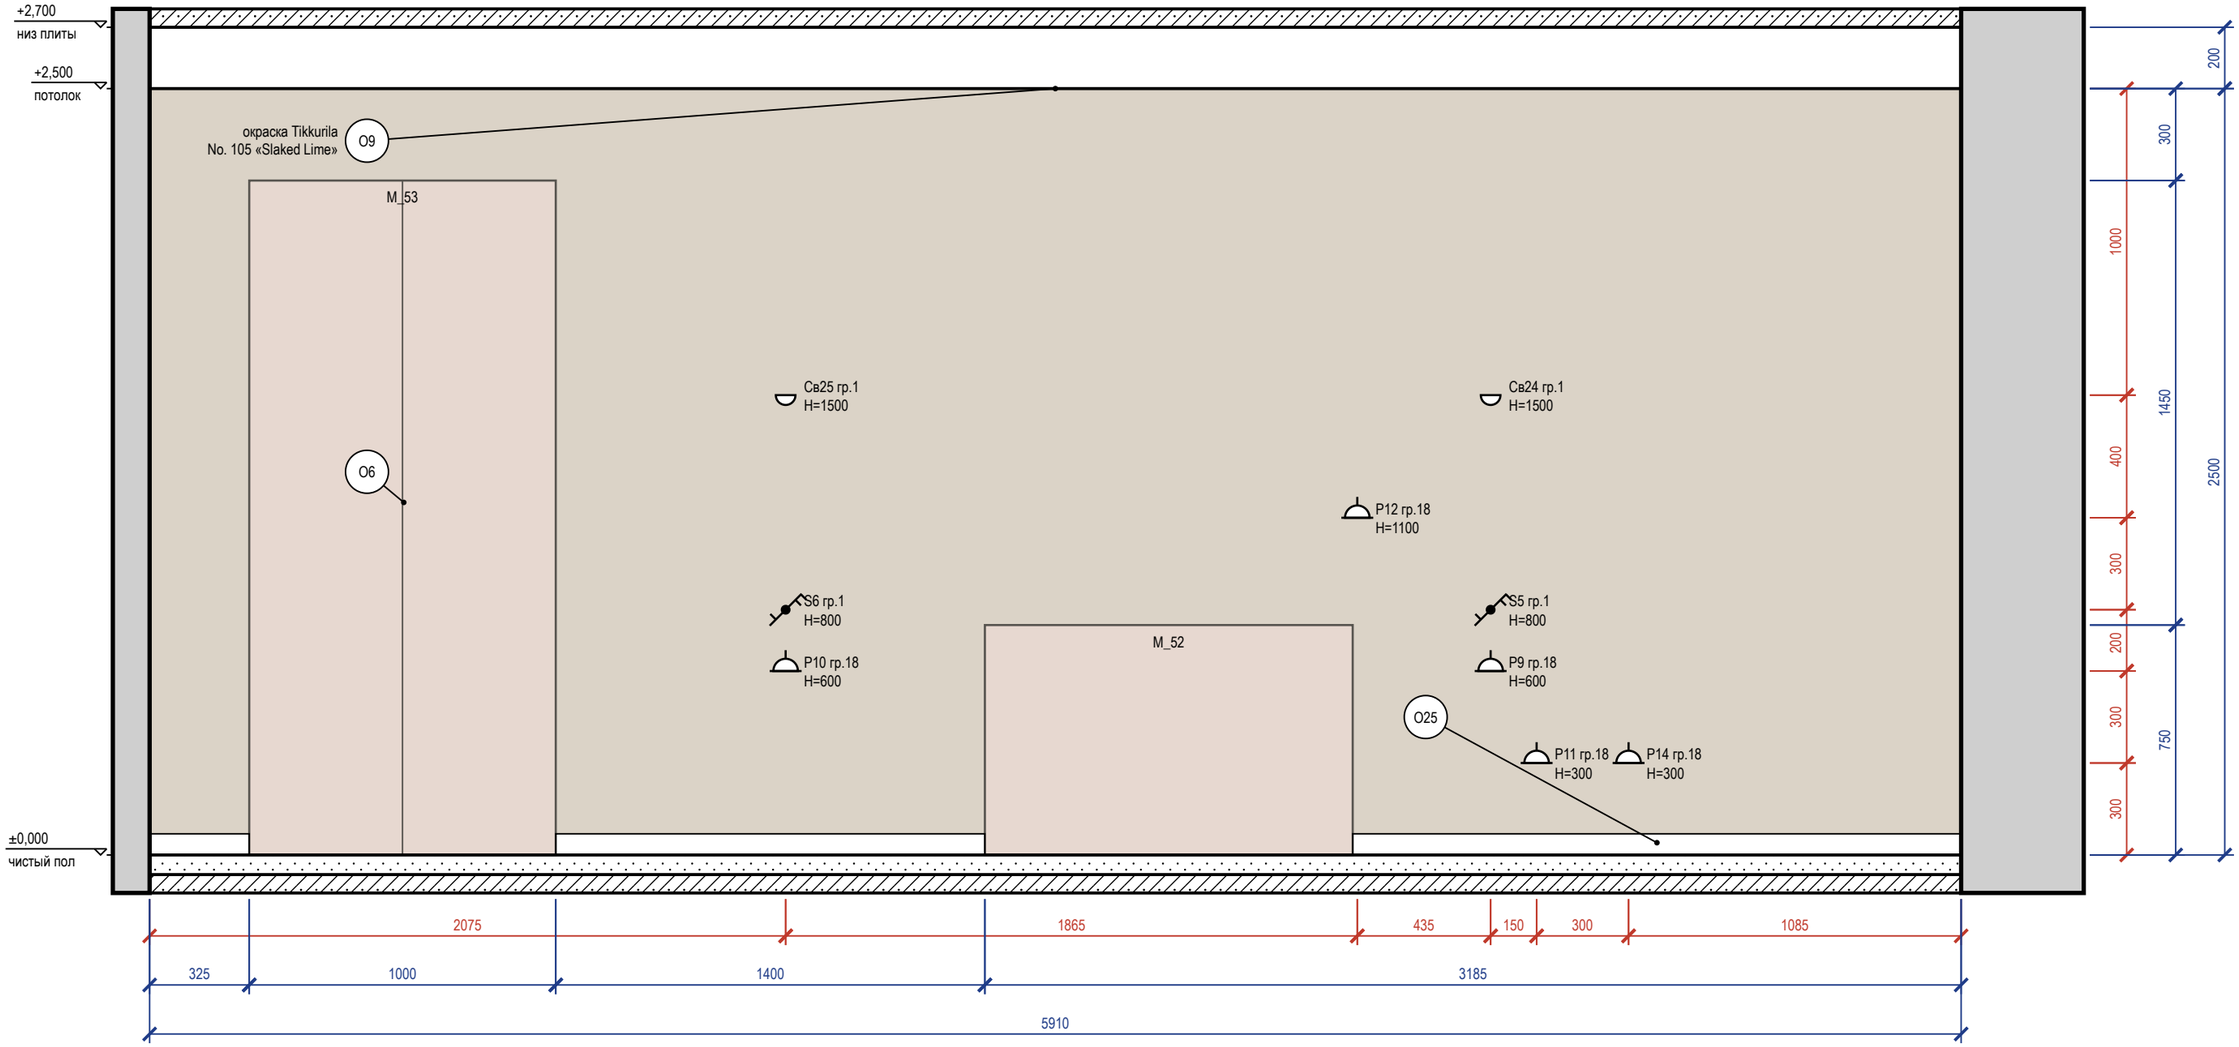


### Схема развёрток (М 1:100)

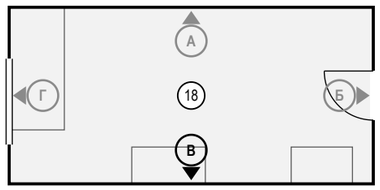


### Ведомость отделки (на листе)

| Марка | Поверхность | Материал, изделие | Цвет, код | Кол. |
|---|---|---|---|---|
| O6 | стены | окраска, Farrow & Ball Modern Emulsion, матовая, подготовка Q3 | Farrow & Ball No. 226 «Joa's White» | 14,8 м² |
| O9 | потолок | окраска, Tikkurila Anti-Reflex 2, глубокоматовая, подготовка Q3 | Little Greene No. 105 «Slaked Lime» | 17,1 м² |
| O25 | плинтус | плинтус МДФ, Orac Decor Contour (Luxxus), h 69 мм, SX165 | Farrow & Ball No. 226 «Joa's White» | 3,7 м |

Визуализация этой стены — лист 128

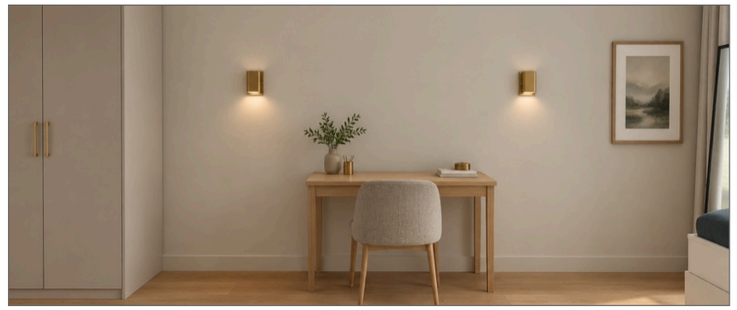

### Примечания

1. Размеры — в мм от чистовых поверхностей стен; условные обозначения и общие указания — лист 2.
2. Потолок на развёртках — по нижнему уровню У1; другие уровни потолка помещения: У2 +2,600.

| | | | | | |
|---|---|---|---|---|---|
| | | | | | Проект: Дом 331 м² |
| | Лист | № док. | Подпись | Дата | Развёртка стены В. Спальня 3 (пом. 18) |
| Дизайнер | Кырлан А.С. | | | 19.10.26 | |

| Стадия | Лист | Листов |
|---|---|---|
| П | 131 | 156 |

выпуск 18.10.2026 № 8cd922c868 · стр. 131 из 156

Правка к этому листу

## Развёртка стены Г

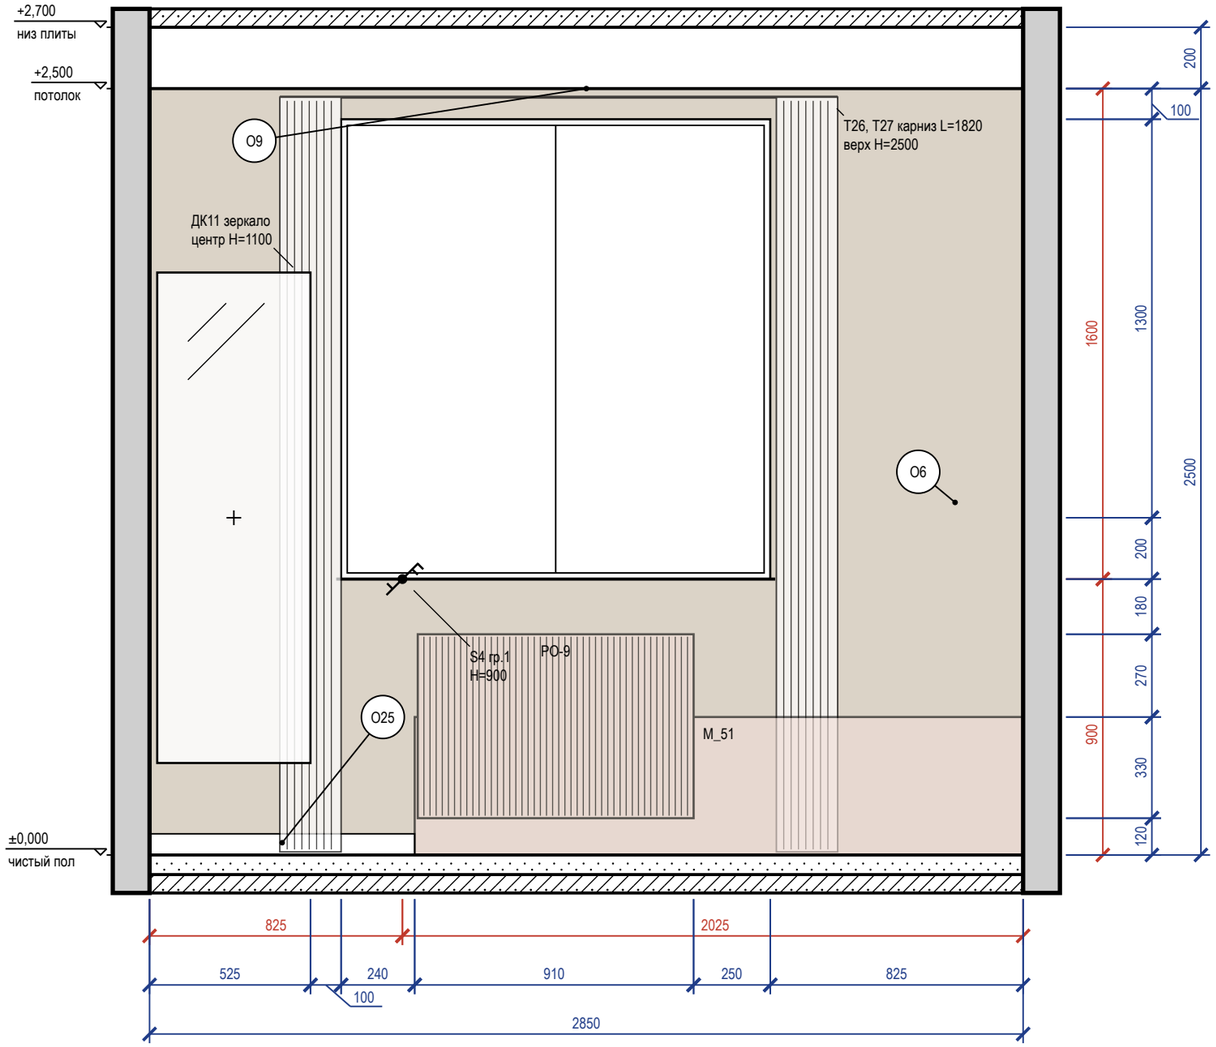


## Схема развёрток (М 1:100)

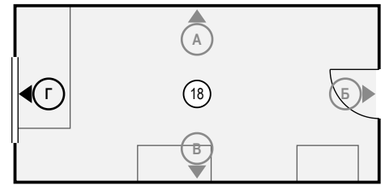


## Ведомость отделки (на листе)

| Марка | Поверхность | Материал, изделие | Цвет, код | Кол. |
|---|---|---|---|---|
| О6 | стены | окраска, Farrow & Ball Modern Emulsion, матовая, подготовка Q3 | Farrow & Ball No. 226 «Joa's White» | 5 м² |
| О9 | потолок | окраска, Tikkurila Anti-Reflex 2, глубокоматовая, подготовка Q3 | Little Greene No. 105 «Slaked Lime» | 17,1 м² |
| О25 | плинтус | плинтус МДФ, Orac Decor Contour (Luxxus), h 69 мм, SX165 | Farrow & Ball No. 226 «Joa's White» | 0,9 м |

Визуализация этой стены

## Примечания

1. Размеры — в мм от чистовых поверхностей стен; условные обозначения и общие указания — лист 2.
2. Картины и зеркала крепить к основанию по паспорту изделия (закладные и анкеры — в перечне скрытых работ); крест — ось центра предмета.
3. Карнизы (шины) — по ведомости текстиля декоратора; длина L и верх H — по развёртке, крепление — до окраски потолка.
4. Потолок на развёртках — по нижнему уровню У1; другие уровни потолка помещения: У2 +2,600.

| | | | | | |
|---|---|---|---|---|---|
| | | | | | Проект: Дом 331 м² |
| | Лист | № док. | Подпись | Дата | Развёртка стены Г. Спальня 3 (пом. 18) |
| Дизайнер | Кырлан А.С. | | | 19.10.26 | |

| Стадия | Лист | Листов |
|---|---|---|
| П | 132 | 156 |

выпуск 18.10.2026 № 8cd922c868 · стр. 132 из 156

Правка к этому листу

| | | | | | |
|---|---|---|---|---|---|
| | | | | | Проект: Дом 331 м² |
| | Лист | № док. | Подпись | Дата | |
| Дизайнер | Кырлан А.С. | | | 19.10.26 | Визуализация: Спальня 4 |

| Стадия | Лист | Листов |
|---|---|---|
| П | 133 | 156 |

выпуск 18.10.2026 № 8cd922c868 · стр. 133 из 156

Правка к этому листу

| | | | | | |
|---|---|---|---|---|---|
| | | | | | Проект: Дом 331 м² |
| | Лист | № док. | Подпись | Дата | |
| Дизайнер | Кырлан А.С. | | | 19.10.26 | Визуализация: Спальня 4 |

| Стадия | Лист | Листов |
|---|---|---|
| П | 134 | 156 |

выпуск 18.10.2026 № 8cd922c868 · стр. 134 из 156

Правка к этому листу

## Развёртка стены А

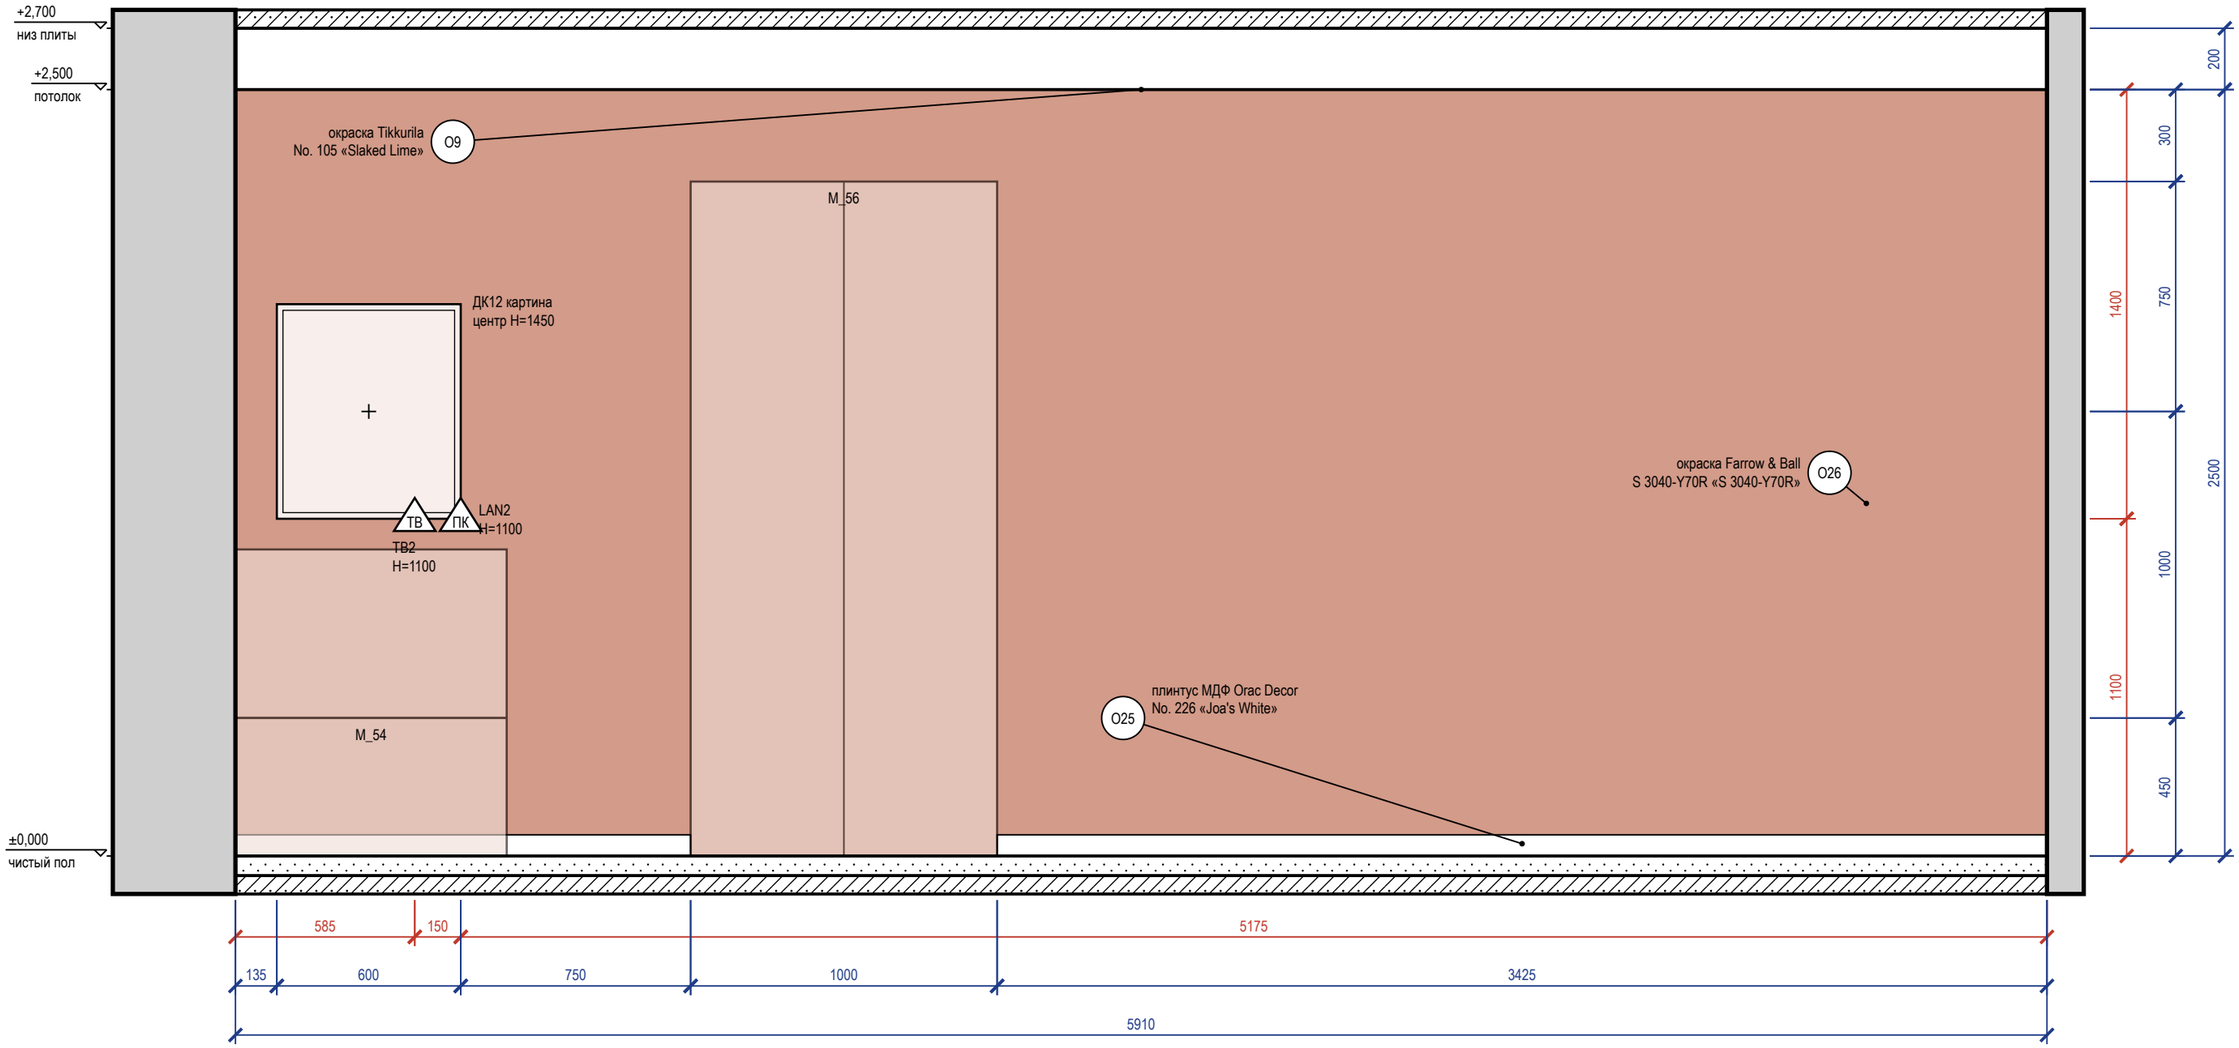


### Схема развёрток (М 1:100)

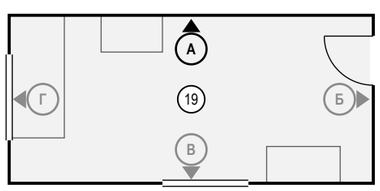


### Ведомость отделки (на листе)

| Марка | Поверхность | Материал, изделие | Цвет, код | Кол. |
|---|---|---|---|---|
| O9 | потолок | окраска, Tikkurila Anti-Reflex 2, глубокоматовая, подготовка Q3 | Little Greene No. 105 «Slaked Lime» | 16,3 м² |
| O25 | плинтус | плинтус МДФ, Orac Decor Contour (Luxxus), h 69 мм, SX165 | Farrow & Ball No. 226 «Joa's White» | 4,9 м |
| O26 | акцентная стена | окраска, Farrow & Ball Modern Emulsion, матовая, подготовка Q3 | NCS S 3040-Y70R «S 3040-Y70R» | 14,8 м² |

Визуализация этой стены — лист 133

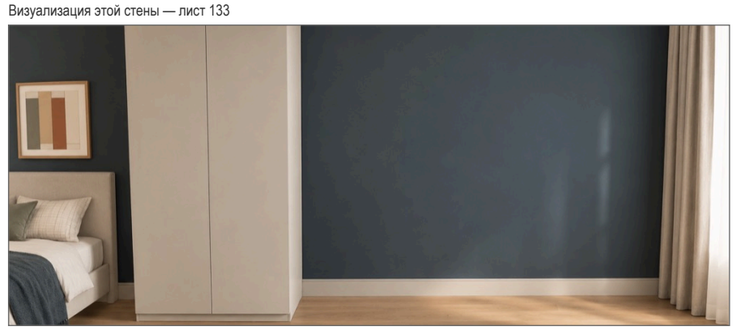

### Примечания

1. Размеры — в мм от чистовых поверхностей стен; условные обозначения и общие указания — лист 2.
2. Картины и зеркала крепить к основанию по паспорту изделия (закладные и анкеры — в перечне скрытых работ); крест — ось центра предмета.
3. Потолок на развёртках — по нижнему уровню У1; другие уровни потолка помещения: У2 +2,600.

| | | | | | |
|---|---|---|---|---|---|
| | | | | | Проект: Дом 331 м² |
| | Лист | № док. | Подпись | Дата | Развёртка стены А. Спальня 4 (пом. 19) |
| Дизайнер | Кырлан А.С. | | | 19.10.26 | |

| Стадия | Лист | Листов |
|---|---|---|
| П | 135 | 156 |

выпуск 18.10.2026 № 8cd922c868 · стр. 135 из 156

Правка к этому листу

## Развёртка стены Б

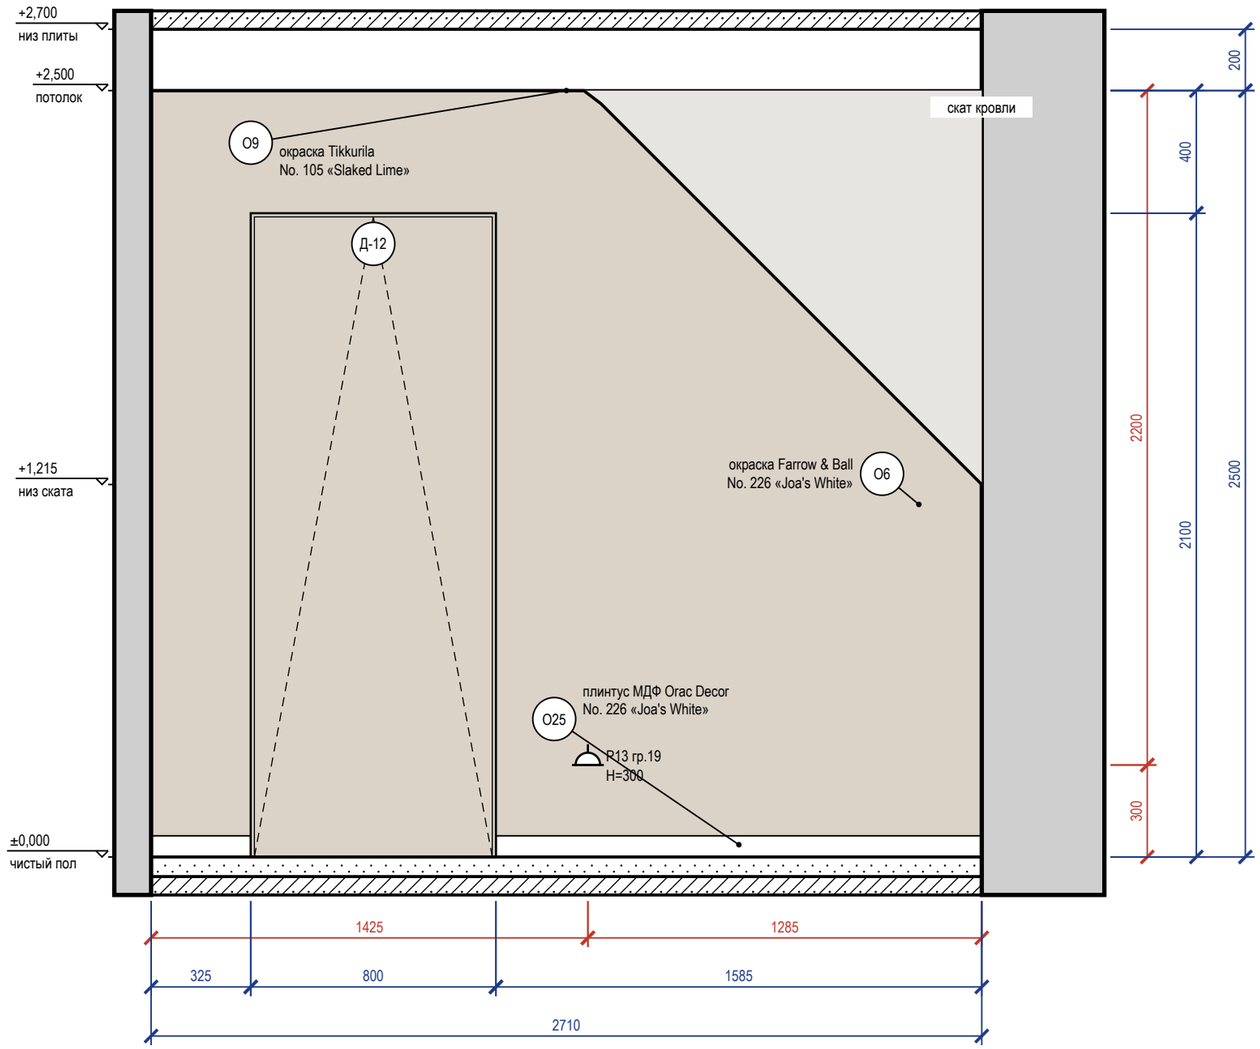


## Схема развёрток (М 1:100)

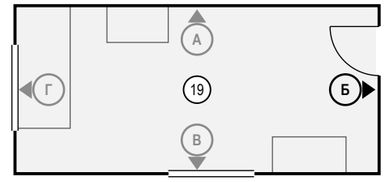


## Ведомость отделки (на листе)

| Марка | Поверхность | Материал, изделие | Цвет, код | Кол. |
|---|---|---|---|---|
| О6 | стены | окраска, Farrow & Ball Modern Emulsion, матовая, подготовка Q3 | Farrow & Ball No. 226 «Joa's White» | 5,1 м² |
| О9 | потолок | окраска, Tikkurila Anti-Reflex 2, глубокоматовая, подготовка Q3 | Little Greene No. 105 «Slaked Lime» | 16,3 м² |
| О25 | плинтус | плинтус МДФ, Orac Decor Contour (Luxxus), h 69 мм, SX165 | Farrow & Ball No. 226 «Joa's White» | 1,9 м |

## Примечания

1. Размеры — в мм от чистовых поверхностей стен; условные обозначения и общие указания — лист 2.
2. Двери скрытого монтажа — полотно в плоскости стены, отделка стены по полотну, плинтус прерывается у короба (узел — на листе узлов).
3. Потолок на развёртках — по нижнему уровню У1; другие уровни потолка помещения: У2 +2,600.

| | | | | | |
|---|---|---|---|---|---|
| | | | | | Проект: Дом 331 м² |
| | Лист | № док. | Подпись | Дата | Развёртка стены Б. Спальня 4 (пом. 19) |
| Дизайнер | Кырлан А.С. | | | 19.10.26 | |

| Стадия | Лист | Листов |
|---|---|---|
| П | 136 | 156 |

выпуск 18.10.2026 № 8cd922c868 · стр. 136 из 156

Правка к этому листу

## Развёртка стены В

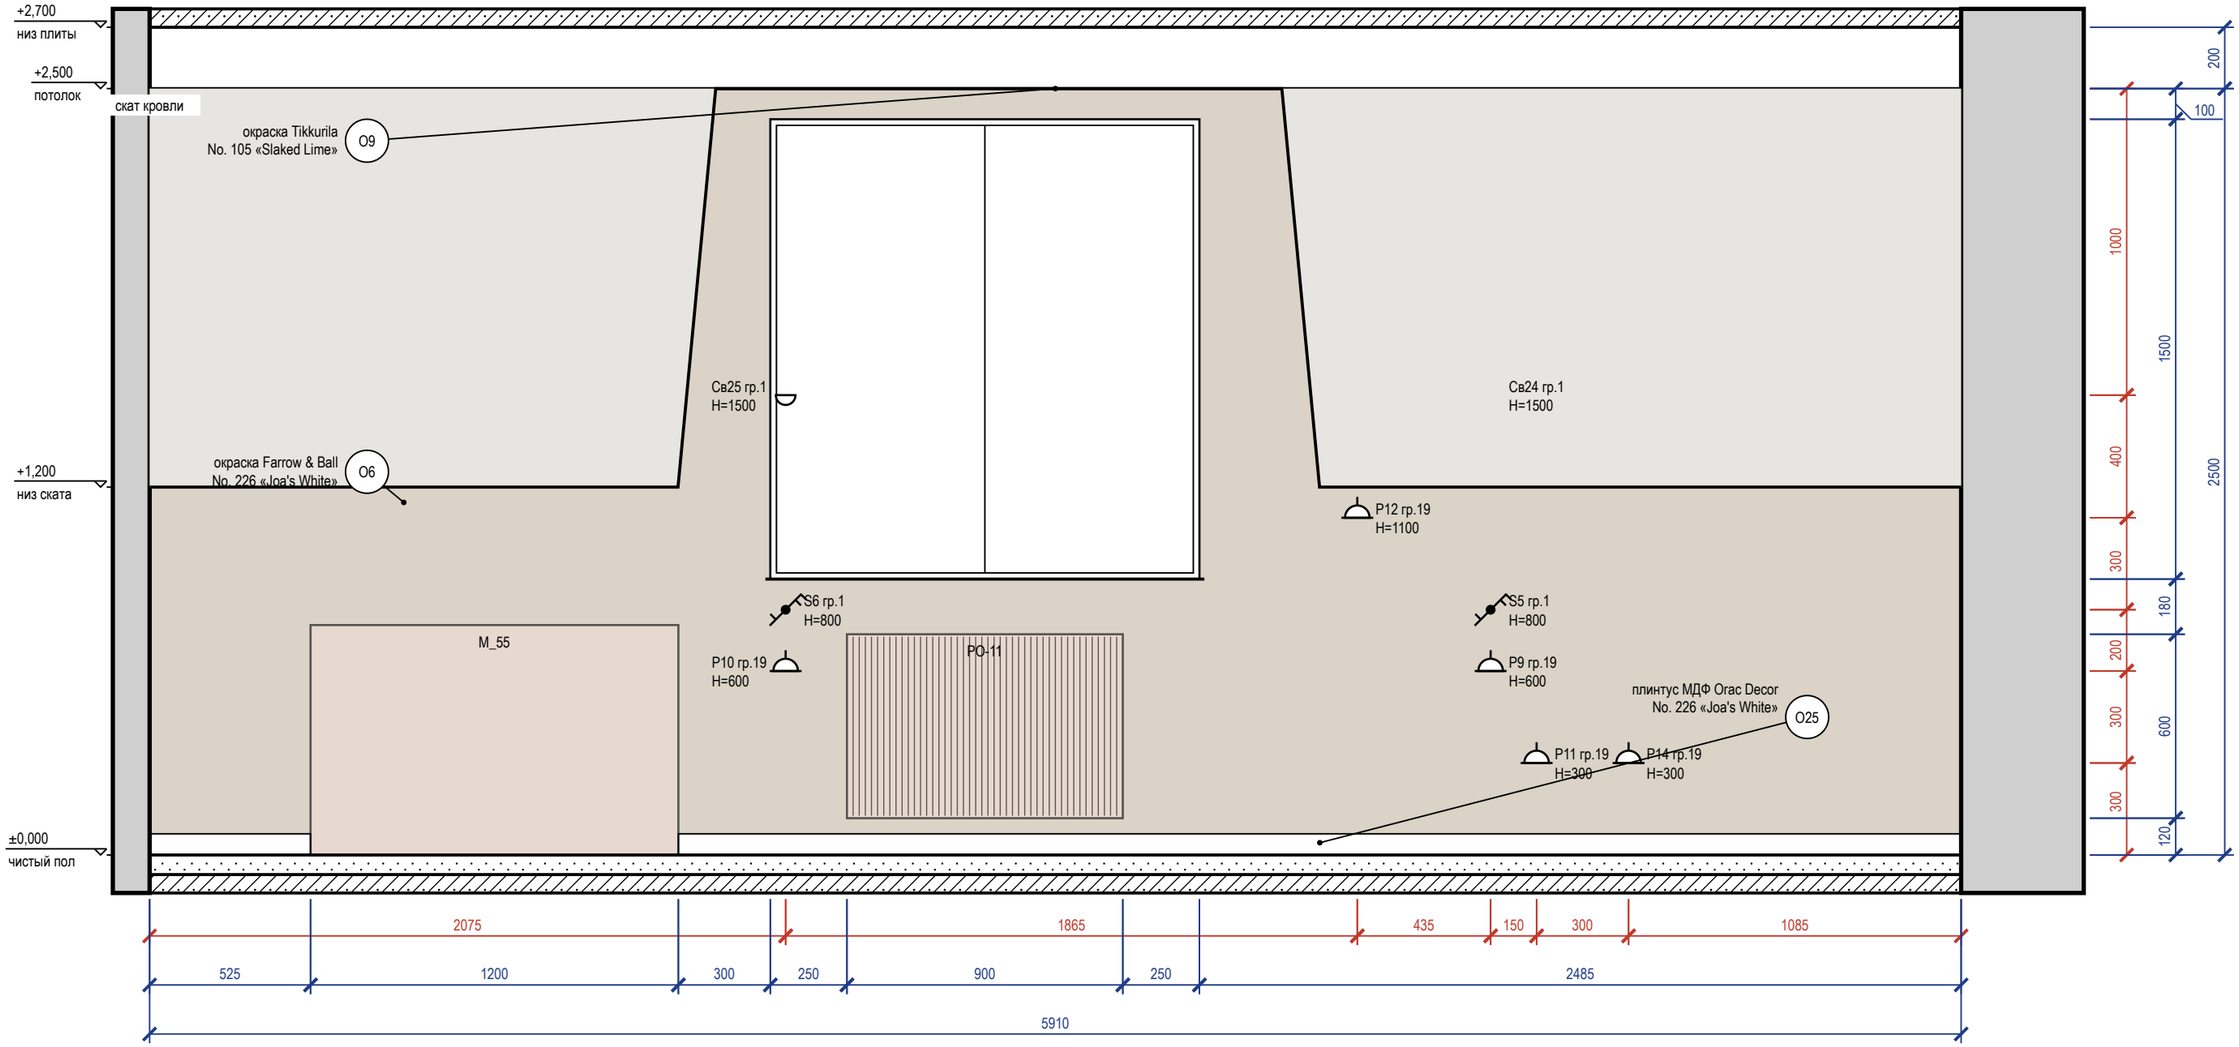


### Схема развёрток (М 1:100)

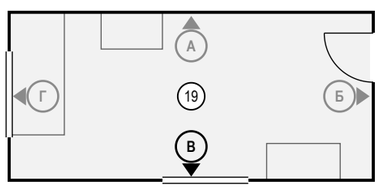


### Ведомость отделки (на листе)

| Марка | Поверхность | Материал, изделие | Цвет, код | Кол. |
|---|---|---|---|---|
| О6 | стены | окраска, Farrow & Ball Modern Emulsion, матовая, подготовка Q3 | Farrow & Ball No. 226 «Joa's White» | 12,7 м² |
| О9 | потолок | окраска, Tikkurila Anti-Reflex 2, глубокоматовая, подготовка Q3 | Little Greene No. 105 «Slaked Lime» | 16,3 м² |
| О25 | плинтус | плинтус МДФ, Orac Decor Contour (Luxxus), h 69 мм, SX165 | Farrow & Ball No. 226 «Joa's White» | 4,7 м |

Визуализация этой стены — лист 134

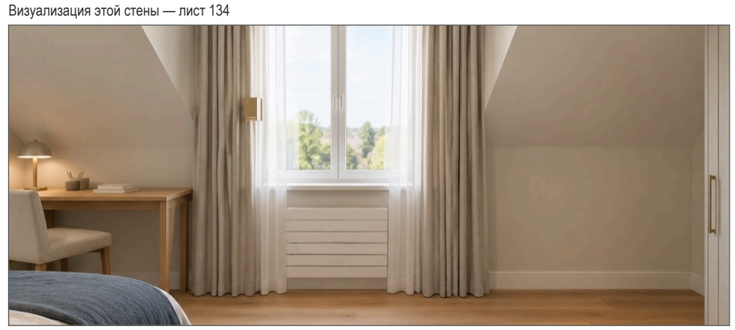

### Примечания

1. Размеры — в мм от чистовых поверхностей стен; условные обозначения и общие указания — лист 2.
2. Потолок на развёртках — по нижнему уровню У1; другие уровни потолка помещения: У2 +2,600.

| | | | | |
|---|---|---|---|---|
| | Лист | № док. | Подпись | Дата |
| Дизайнер | Кырлан А.С. | | | 19.10.26 |

Проект: Дом 331 м²

Развёртка стены В. Спальня 4 (пом. 19)

| Стадия | Лист | Листов |
|---|---|---|
| П | 137 | 156 |

выпуск 18.10.2026 № 8cd922c868 · стр. 137 из 156

Правка к этому листу

## Развёртка стены Г

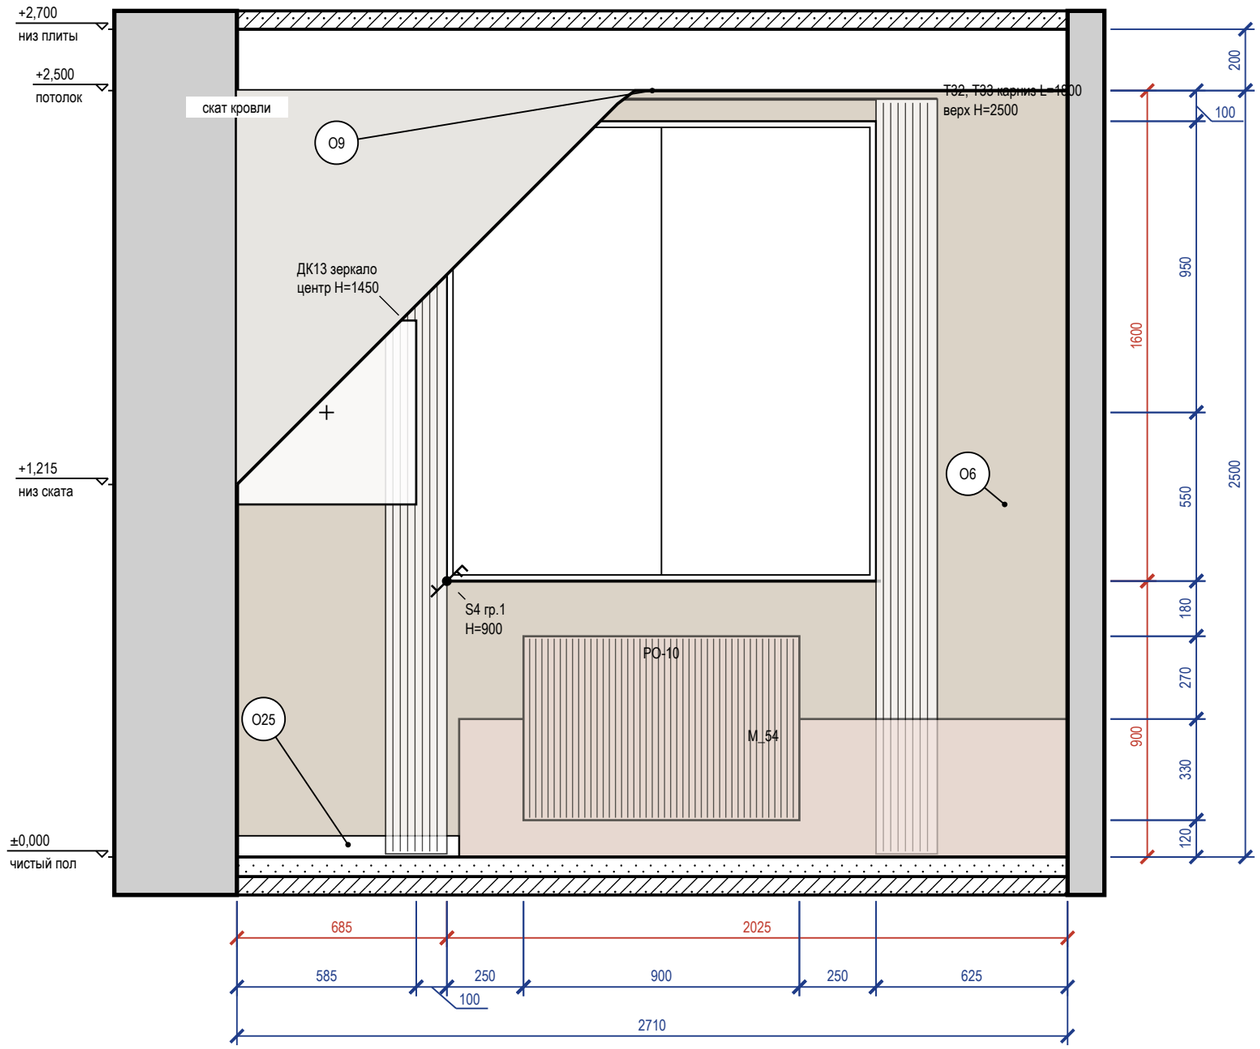


## Схема развёрток (М 1:100)

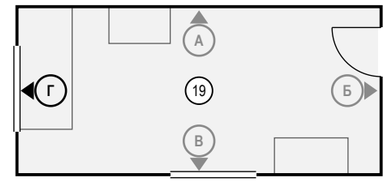


## Ведомость отделки (на листе)

| Марка | Поверхность | Материал, изделие | Цвет, код | Кол. |
|---|---|---|---|---|
| О6 | стены | окраска, Farrow & Ball Modern Emulsion, матовая, подготовка Q3 | Farrow & Ball No. 226 «Joa's White» | 4,7 м² |
| О9 | потолок | окраска, Tikkurila Anti-Reflex 2, глубокоматовая, подготовка Q3 | Little Greene No. 105 «Slaked Lime» | 16,3 м² |
| О25 | плинтус | плинтус МДФ, Orac Decor Contour (Luxxus), h 69 мм, SX165 | Farrow & Ball No. 226 «Joa's White» | 0,7 м |

## Примечания

1. Размеры — в мм от чистовых поверхностей стен; условные обозначения и общие указания — лист 2.
2. Картины и зеркала крепить к основанию по паспорту изделия (закладные и анкеры — в перечне скрытых работ); крест — ось центра предмета.
3. Карнизы (шины) — по ведомости текстиля декоратора; длина L и верх H — по развёртке, крепление — до окраски потолка.
4. Потолок на развёртках — по нижнему уровню У1; другие уровни потолка помещения: У2 +2,600.

| | | | | | |
|---|---|---|---|---|---|
| | | | | | Проект: Дом 331 м² |
| | Лист | № док. | Подпись | Дата | |
| Дизайнер | Кырлан А.С. | | | 19.10.26 | Развёртка стены Г. Спальня 4 (пом. 19) |

| Стадия | Лист | Листов |
|---|---|---|
| П | 138 | 156 |

выпуск 18.10.2026 № 8cd922c868 · стр. 138 из 156

Правка к этому листу

| | | | | | |
|---|---|---|---|---|---|
| | | | | | Проект: Дом 331 м² |
| | Лист | № док. | Подпись | Дата | |
| Дизайнер | Кырлан А.С. | | | 19.10.26 | Визуализация: Санузел 2 |

| Стадия | Лист | Листов |
|---|---|---|
| П | 139 | 156 |

выпуск 18.10.2026 № 8cd922c868 · стр. 139 из 156

Правка к этому листу

## Развёртка стены А

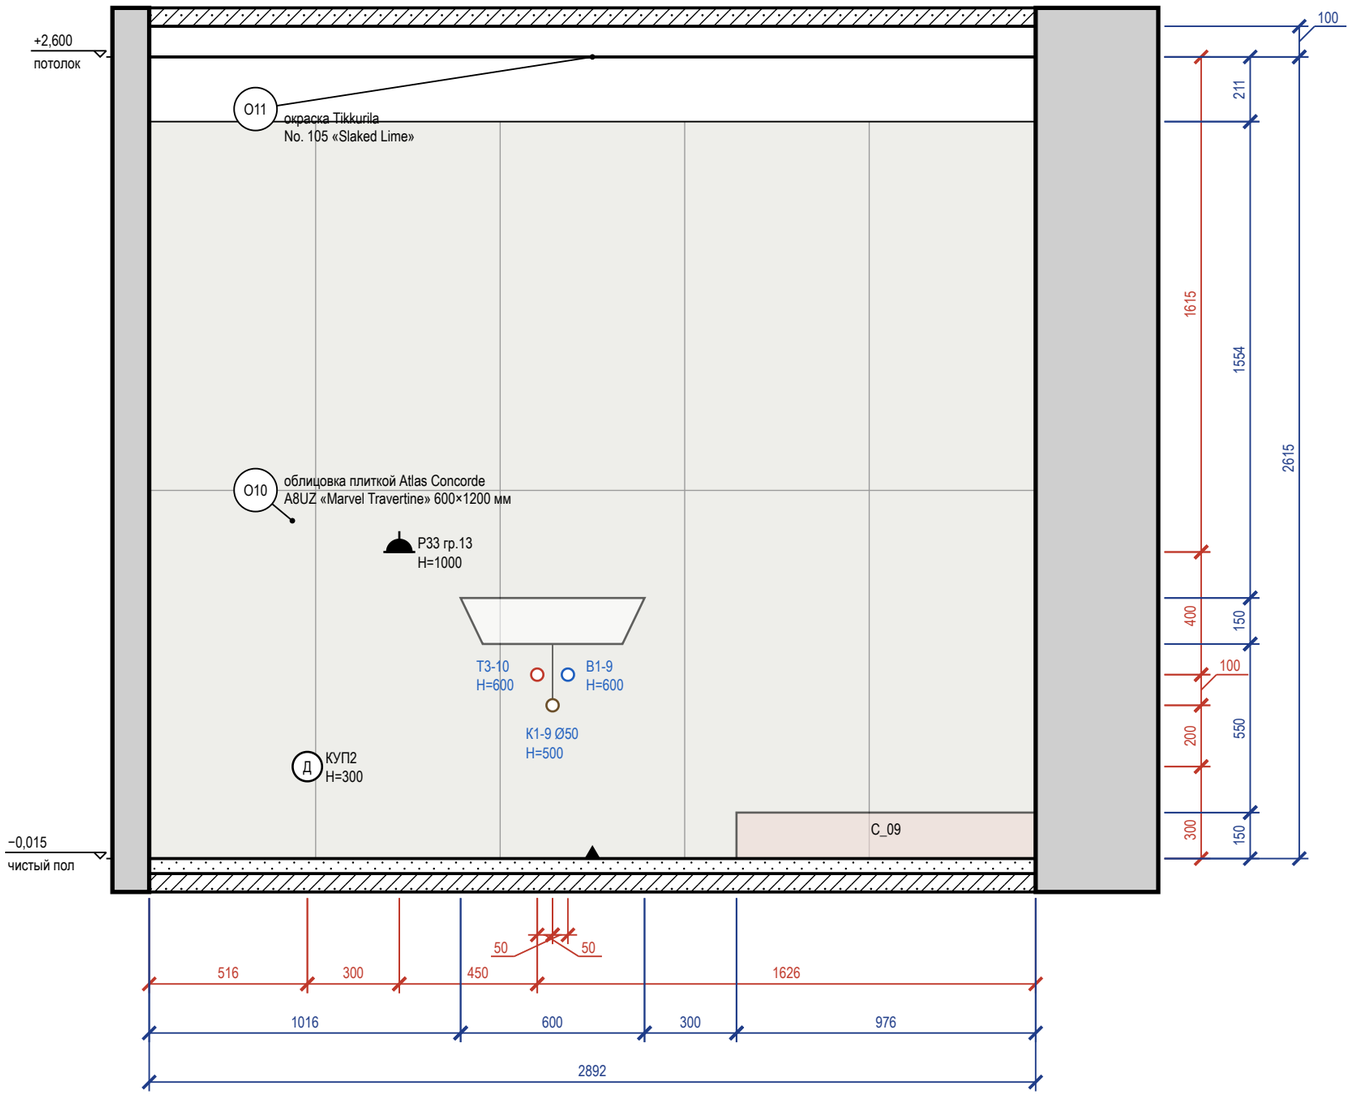


## Схема развёрток (М 1:100)

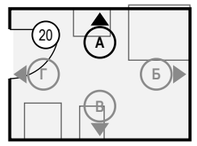


## Ведомость отделки (на листе)

| Марка | Поверхность | Материал, изделие | Цвет, код | Кол. |
|---|---|---|---|---|
| О10 | стены | облицовка плиткой, Atlas Concorde Marvel Travertine, 600×1200×9 мм, A8UZ, затирка CG2WA | Atlas Concorde A8UZ «Marvel Travertine» | 7 м² |
| О11 | потолок | окраска, Tikkurila Luja 7, матовая, подготовка Q3 | Little Greene No. 105 «Slaked Lime» | 6,3 м² |

## Примечания

1. Размеры — в мм от чистовых поверхностей стен; условные обозначения и общие указания — лист 2.
2. Схема мебели, приборов и декора не является технической документацией для производства мебели; габариты — по паспортам изделий.
3. Выводы ВК — коды и высоты по листу выводов сантехники.
4. Облицовка — по сетке швов 2 мм, раскладка от оси стены (треугольник у пола), целые ряды от пола; подрезки — по листу раскладки плитки.
5. Гидроизоляция в 2 слоя, заход на стены 200 мм — до облицовки, с актом скрытых работ и тестом проливом (узел — на листе узлов).

| | | | | | |
|---|---|---|---|---|---|
| | | | | | Проект: Дом 331 м² |
| | Лист | № док. | Подпись | Дата | Развёртка стены А. Санузел 2 (пом. 20) |
| Дизайнер | Кырлан А.С. | | | 19.10.26 | |

| Стадия | Лист | Листов |
|---|---|---|
| П | 140 | 156 |

выпуск 18.10.2026 № 8cd922c868 · стр. 140 из 156

## Развёртка стены Б

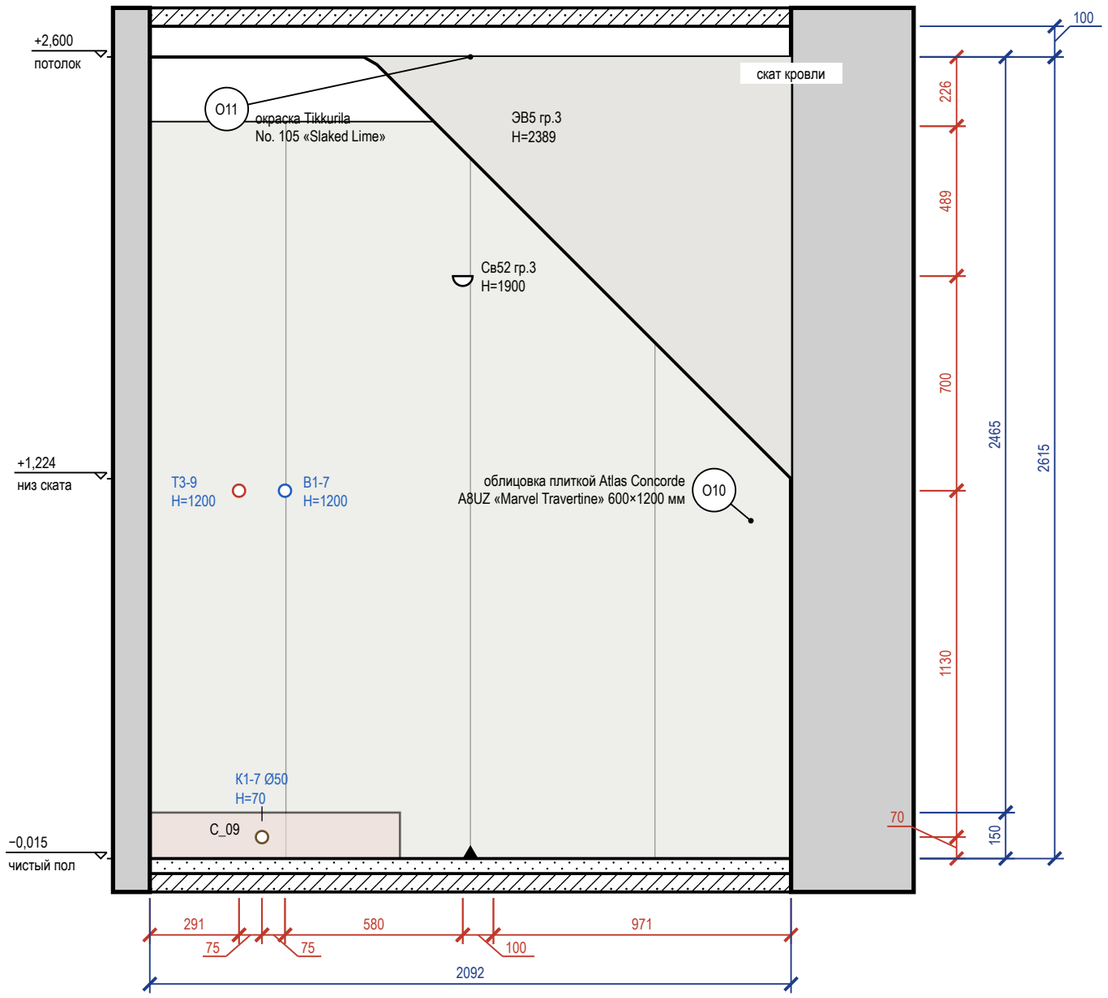


## Схема развёрток (М 1:100)

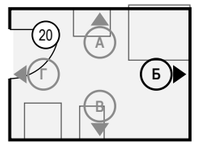


## Ведомость отделки (на листе)

| Марка | Поверхность | Материал, изделие | Цвет, код | Кол. |
|---|---|---|---|---|
| О10 | стены | облицовка плиткой, Atlas Concorde Marvel Travertine, 600×1200×9 мм, A8UZ, затирка CG2WA | Atlas Concorde A8UZ «Marvel Travertine» | 5 м² |
| О11 | потолок | окраска, Tikkurila Luja 7, матовая, подготовка Q3 | Little Greene No. 105 «Slaked Lime» | 6,3 м² |

Визуализация этой стены — лист 139

## Примечания

1. Размеры — в мм от чистовых поверхностей стен; условные обозначения и общие указания — лист 2.
2. Схема мебели, приборов и декора не является технической документацией для производства мебели; габариты — по паспортам изделий.
3. Выводы ВК — коды и высоты по листу выводов сантехники.
4. Облицовка — по сетке швов 2 мм, раскладка от оси стены (треугольник у пола), целые ряды от пола; подрезки — по листу раскладки плитки.
5. Гидроизоляция в 2 слоя, заход на стены 200 мм — до облицовки, с актом скрытых работ и тестом проливом (узел — на листе узлов).

| | | | | | |
|---|---|---|---|---|---|
| | | | | | Проект: Дом 331 м² |
| | Лист | № док. | Подпись | Дата | Развёртка стены Б. Санузел 2 (пом. 20) |
| Дизайнер | Кырлан А.С. | | | 19.10.26 | |

| Стадия | Лист | Листов |
|---|---|---|
| П | 141 | 156 |

Правка к этому листу

## Развёртка стены В

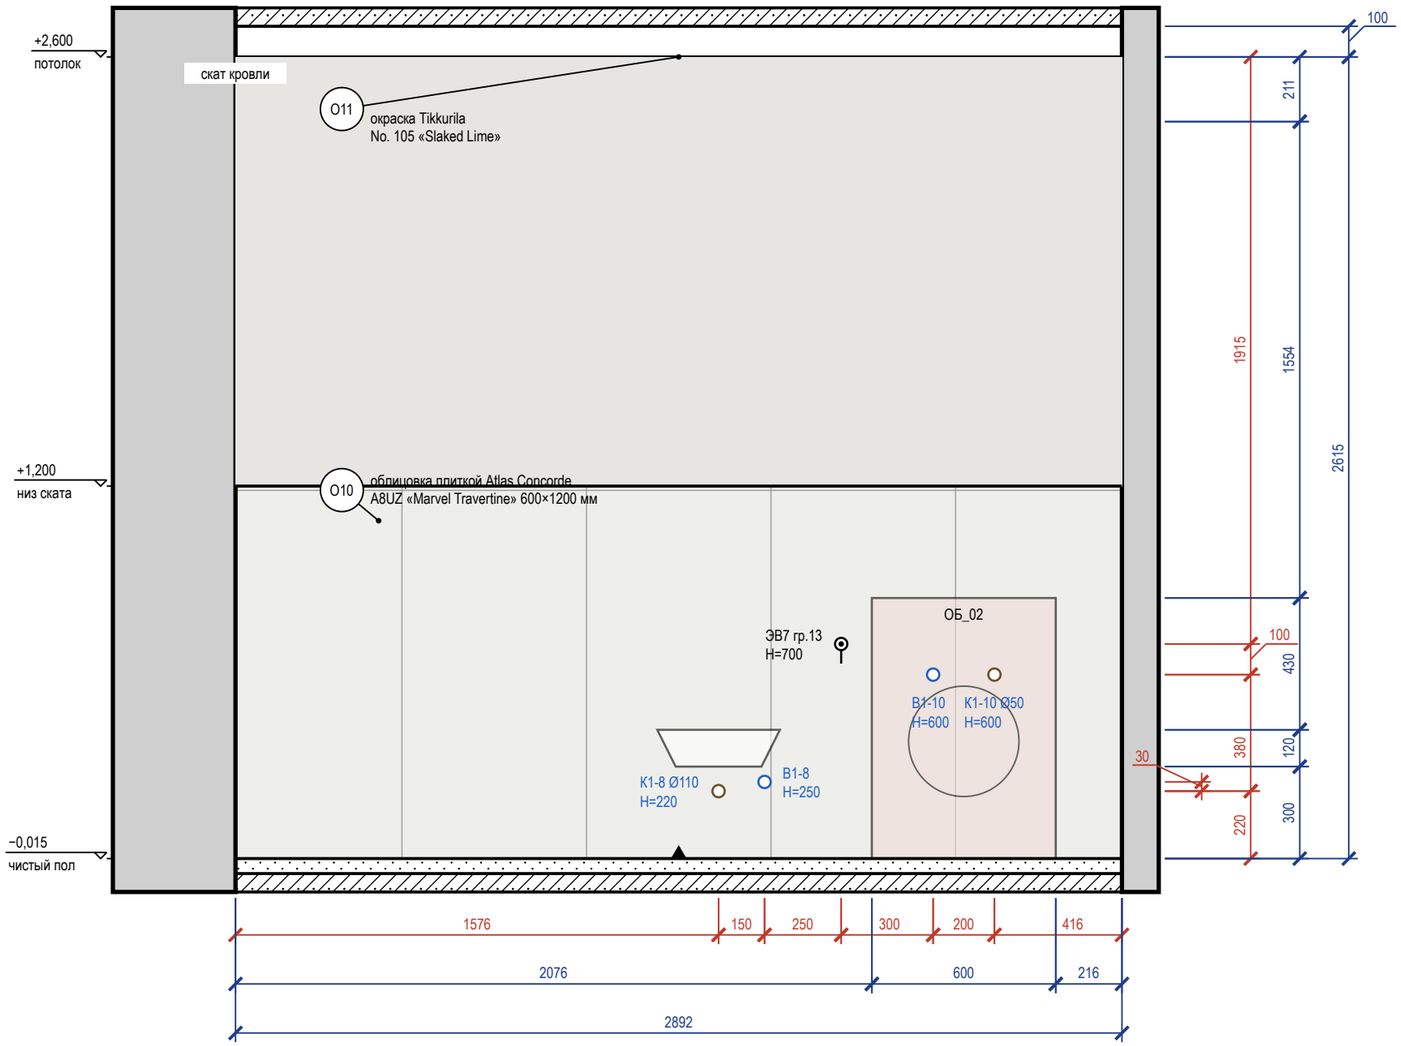


## Схема развёрток (М 1:100)

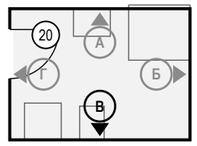


## Ведомость отделки (на листе)

| Марка | Поверхность | Материал, изделие | Цвет, код | Кол. |
|---|---|---|---|---|
| О10 | стены | облицовка плиткой, Atlas Concorde Marvel Travertine, 600×1200×9 мм, A8UZ, затирка CG2WA | Atlas Concorde A8UZ «Marvel Travertine» | 7 м² |
| О11 | потолок | окраска, Tikkurila Luja 7, матовая, подготовка Q3 | Little Greene No. 105 «Slaked Lime» | 6,3 м² |

## Примечания

1. Размеры — в мм от чистовых поверхностей стен; условные обозначения и общие указания — лист 2.
2. Схема мебели, приборов и декора не является технической документацией для производства мебели; габариты — по паспортам изделий.
3. Выводы ВК — коды и высоты по листу выводов сантехники.
4. Облицовка — по сетке швов 2 мм, раскладка от оси стены (треугольник у пола), целые ряды от пола; подрезки — по листу раскладки плитки.
5. Гидроизоляция в 2 слоя, заход на стены 200 мм — до облицовки, с актом скрытых работ и тестом проливом (узел — на листе узлов).

| | | | | | |
|---|---|---|---|---|---|
| | | | | | Проект: Дом 331 м² |
| | Лист | № док. | Подпись | Дата | Развёртка стены В. Санузел 2 (пом. 20) |
| Дизайнер | Кырлан А.С. | | | 19.10.26 | |

| Стадия | Лист | Листов |
|---|---|---|
| П | 142 | 156 |

выпуск 18.10.2026 № 8cd922c868 · стр. 142 из 156

Правка к этому листу

## Развёртка стены Г

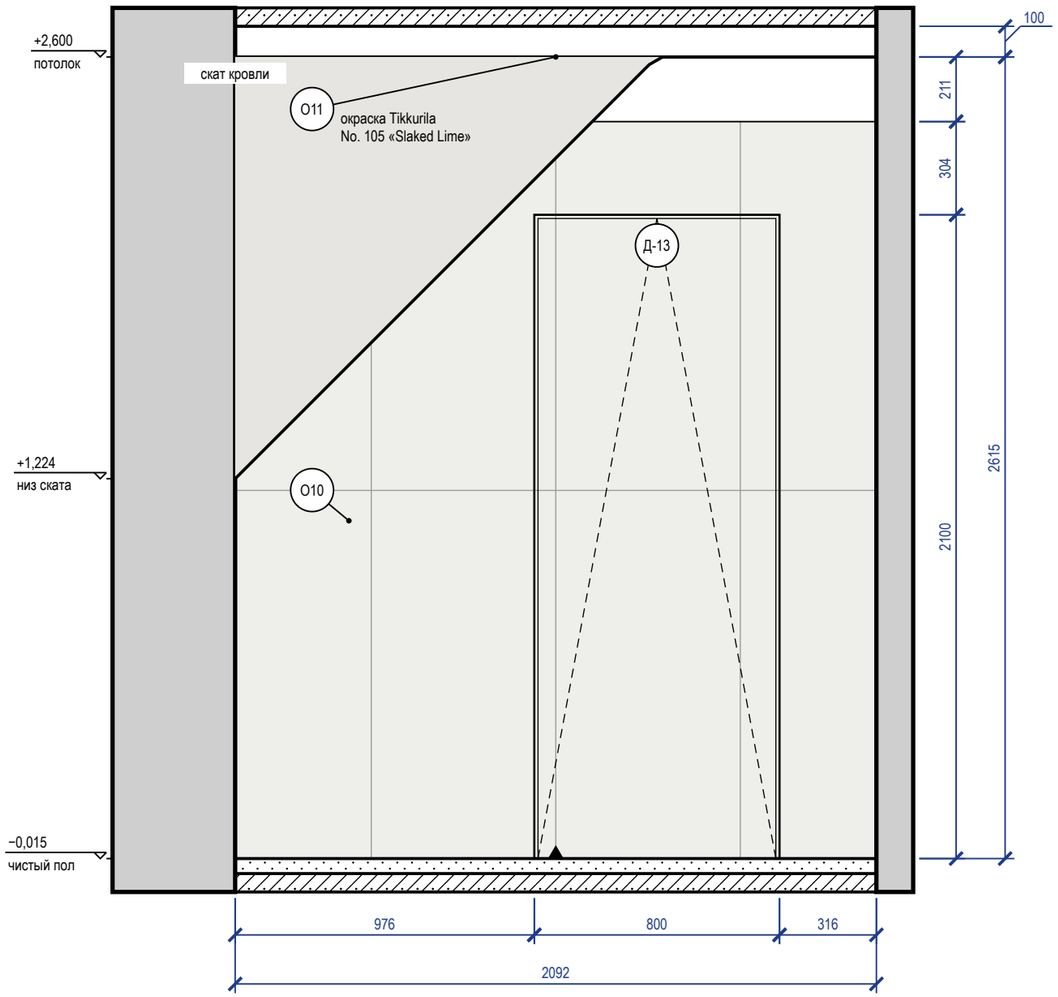


## Схема развёрток (М 1:100)

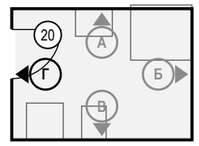


## Ведомость отделки (на листе)

| Марка | Поверхность | Материал, изделие | Цвет, код | Кол. |
|---|---|---|---|---|
| О10 | стены | облицовка плиткой, Atlas Concorde Marvel Travertine, 600×1200×9 мм, A8UZ, затирка CG2WA | Atlas Concorde A8UZ «Marvel Travertine» | 3,3 м² |
| О11 | потолок | окраска, Tikkurila Luja 7, матовая, подготовка Q3 | Little Greene No. 105 «Slaked Lime» | 6,3 м² |

## Примечания

1. Размеры — в мм от чистовых поверхностей стен; условные обозначения и общие указания — лист 2.
2. Облицовка — по сетке швов 2 мм, раскладка от оси стены (треугольник у пола), целые ряды от пола; подрезки — по листу раскладки плитки.
3. Гидроизоляция в 2 слоя, заход на стены 200 мм — до облицовки, с актом скрытых работ и тестом проливом (узел — на листе узлов).
4. Двери скрытого монтажа — полотно в плоскости стены, отделка стены по полотну, плинтус прерывается у короба (узел — на листе узлов).

| | | | | | |
|---|---|---|---|---|---|
| | | | | | Проект: Дом 331 м² |
| | Лист | № док. | Подпись | Дата | Развёртка стены Г. Санузел 2 (пом. 20) |
| Дизайнер | Кырлан А.С. | | | 19.10.26 | |

| Стадия | Лист | Листов |
|---|---|---|
| П | 143 | 156 |

Правка к этому листу

## Общий вид

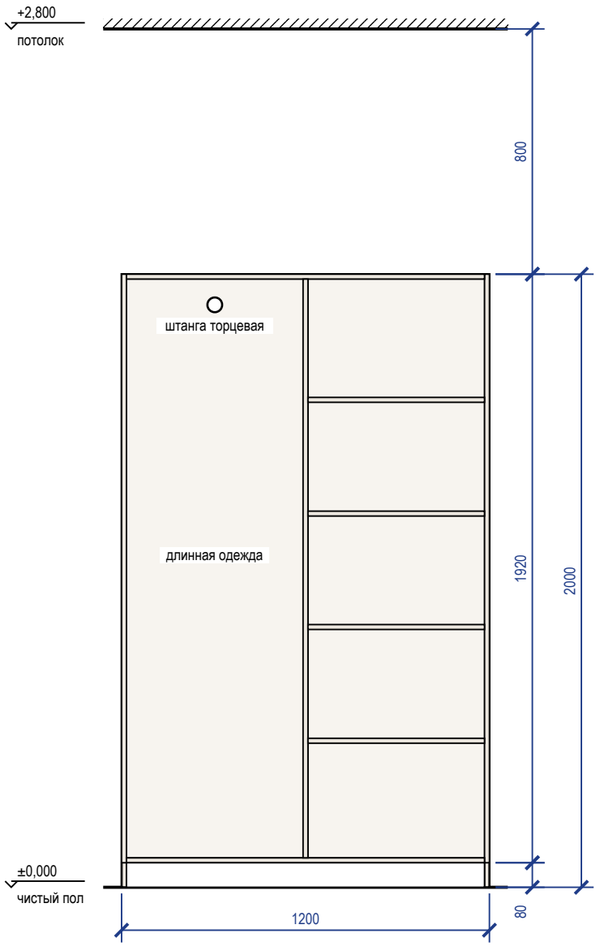


## Наполнение, размеры в свету

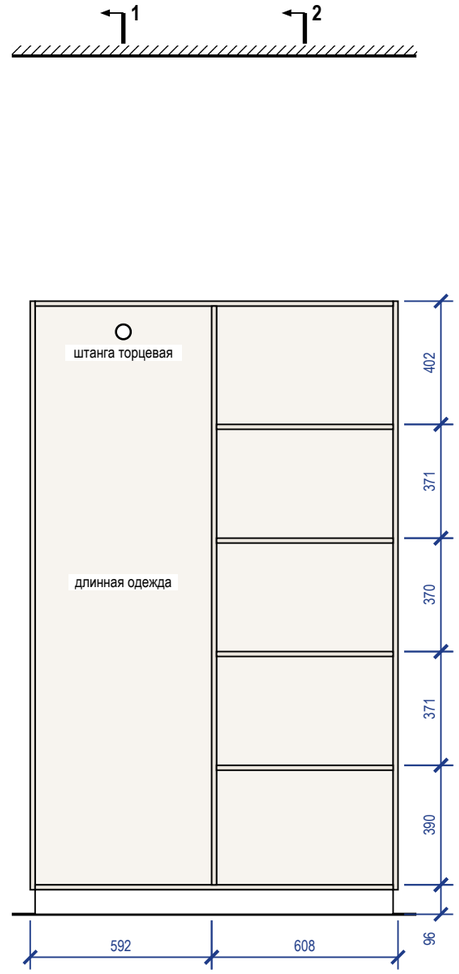


## Разрез 1-1

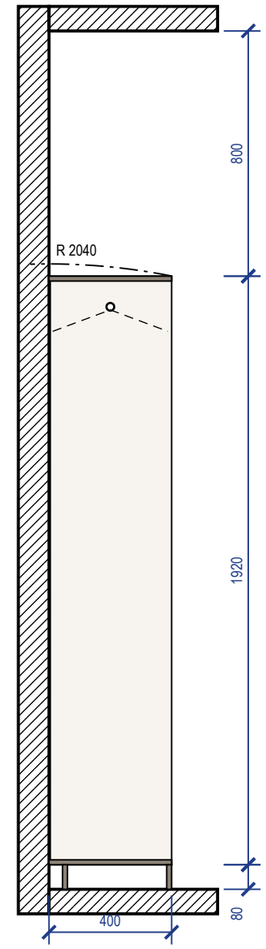


## Разрез 2-2

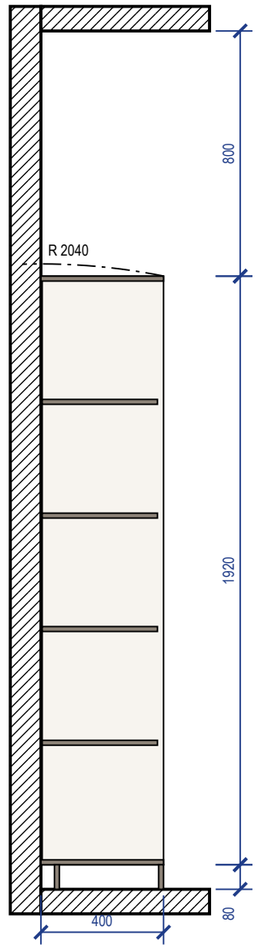


### Примечания

1. Размеры — в мм по чистовой отделке; изделие 1200×400×2000 (Ш×Г×В). Перед раскроем — контрольный замер цеха после чистовой отделки стен, пола и потолка.
2. Корпус — ЛДСП 16 мм, задняя стенка ХДФ 4 мм в паз, цоколь 80 мм на регулируемых опорах; открытая система без фасадов, ящики с фасадами.
3. Кромка: скрытые торцы 0,4 мм, видимые 2 мм (ПВХ/АБС).
4. Номинальные зазоры: между фасадами ящиков 3 мм, фасад ящика — стойка 2 мм.
5. Ящики — направляющие полного выдвижения NL 350 (внутренняя глубина 396 мм ≥ NL + 3); присадка по 32-й системе — выполняет цех.
6. Зазор до потолка 800 мм.
7. Подъём корпуса: диагональ боковины $\sqrt{(2000^2 + 400^2)} = 2040$ мм < 2800 мм до потолка — корпус собирается лёжа и поднимается поворотом.
8. Крепление к стене от опрокидывания — уголки 2 шт. к несущему основанию (монтажная схема шкафов).

## 3D орто

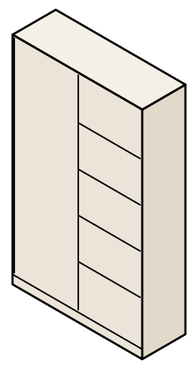

| | | | | | |
|---|---|---|---|---|---|
| | | | | | Проект: Дом 331 м² |
| | Лист | № док. | Подпись | Дата | Система хранения M_17 |
| Дизайнер | Кырлан А.С. | | | 19.10.26 | |

| Стадия | Лист | Листов |
|---|---|---|
| П | Д_1 | 156 |

выпуск 18.10.2026 № 8cd922c868 · стр. 144 из 156

Правка к этому листу

## Общий вид

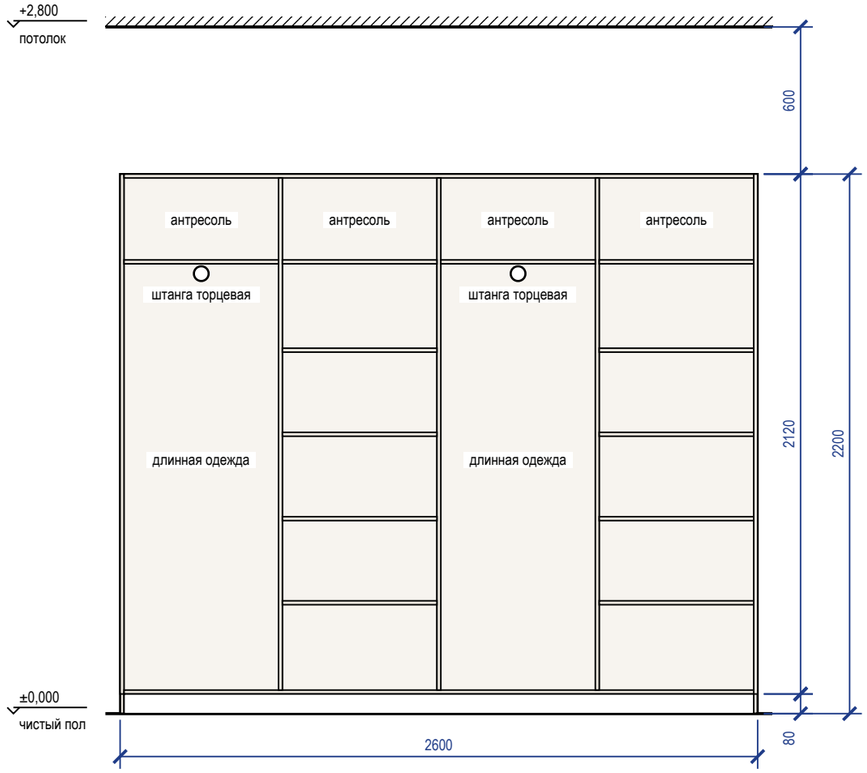


## Наполнение, размеры в свету

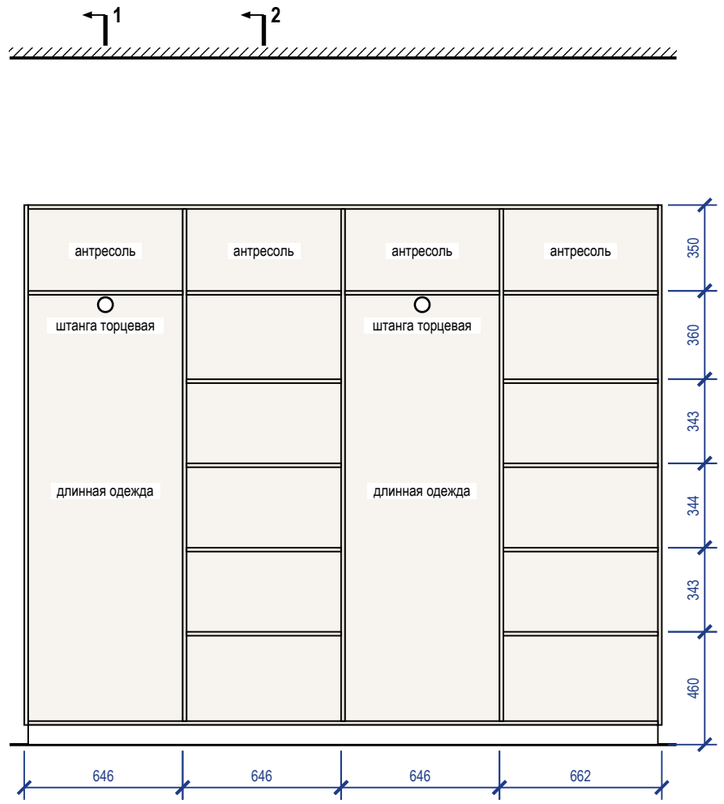


## Разрез 1-1

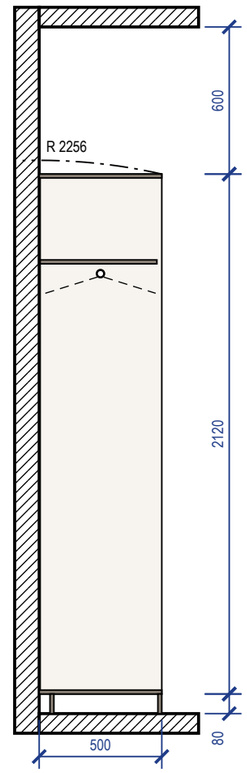


## Разрез 2-2

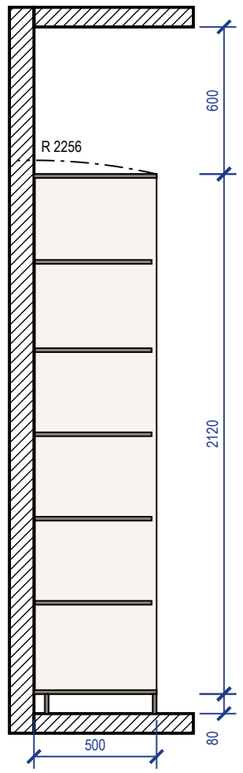


### Примечания

1. Размеры — в мм по чистовой отделке; изделие 2600×500×2200 (Ш×Г×В). Перед раскроем — контрольный замер цеха после чистовой отделки стен, пола и потолка.
2. Корпус — ЛДСП 16 мм, задняя стенка ХДФ 4 мм в паз, цоколь 80 мм на регулируемых опорах; открытая система без фасадов, ящики с фасадами.
3. Кромка: скрытые торцы 0,4 мм, видимые 2 мм (ПВХ/АБС).
4. Номинальные зазоры: между фасадами ящиков 3 мм, фасад ящика — стойка 2 мм.
5. Ящики — направляющие полного выдвижения NL 450 (внутренняя глубина 496 мм ≥ NL + 3); присадка по 32-й системе — выполняет цех.
6. Зазор до потолка 600 мм.
7. Подъём корпуса: диагональ боковины $\sqrt{(2200^2 + 500^2)} = 2256$ мм < 2800 мм до потолка — корпус собирается лёжа и поднимается поворотом.
8. Крепление к стене от опрокидывания — уголки 2 шт. к несущему основанию (монтажная схема шкафов).

## 3D орто

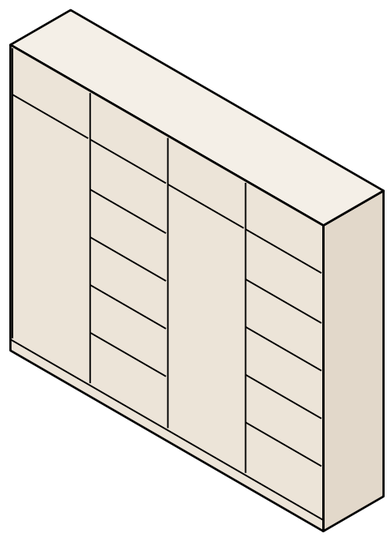

| | | | | | |
|---|---|---|---|---|---|
| | | | | | Проект: Дом 331 м² |
| | Лист | № док. | Подпись | Дата | |
| Дизайнер | Кырлан А.С. | | | 19.10.26 | Система хранения M_23 |
| | | | | | |

| Стадия | Лист | Листов |
|---|---|---|
| П | Д_2 | 156 |

выпуск 18.10.2026 № 8cd922c868 · стр. 145 из 156

Правка к этому листу

## Вид с фасадами

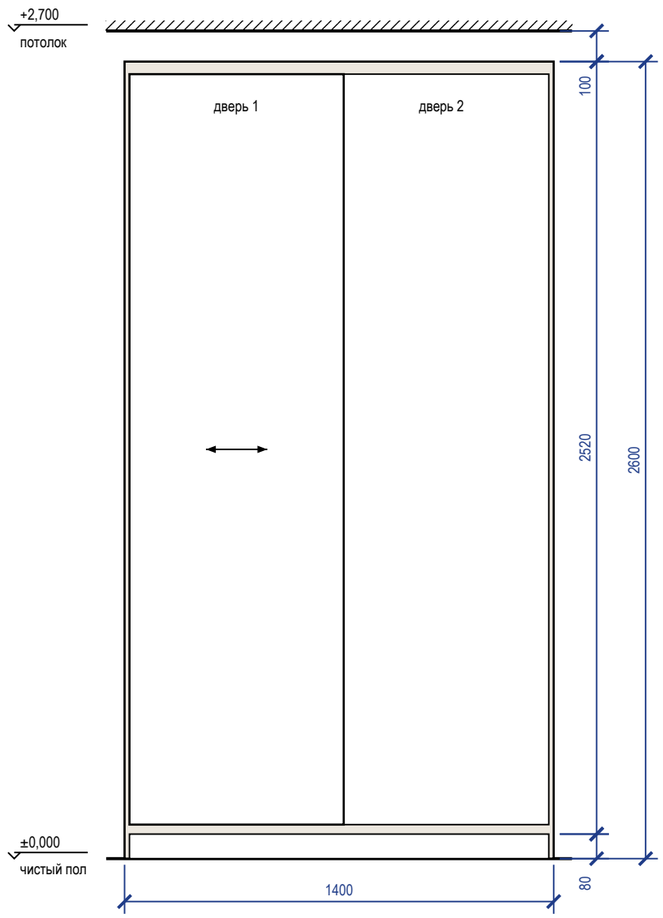


## Вид без фасадов

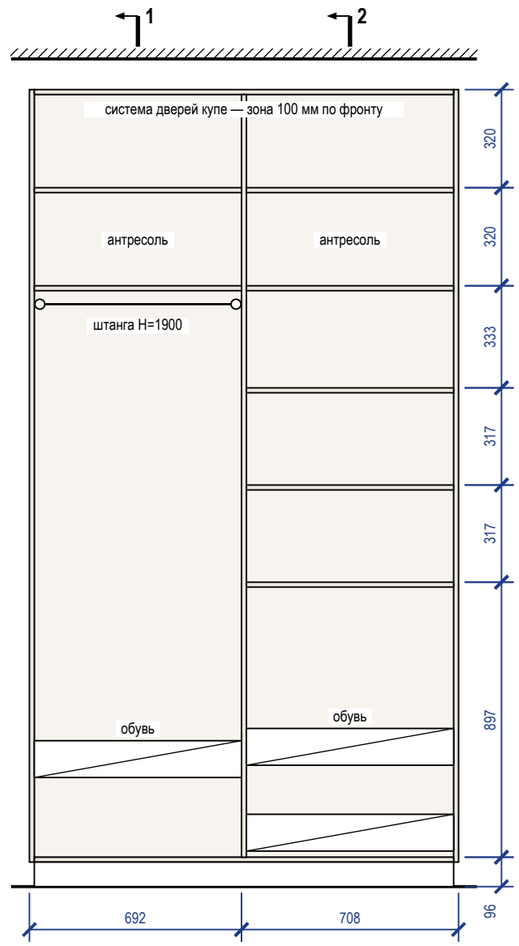


## Разрез 1-1

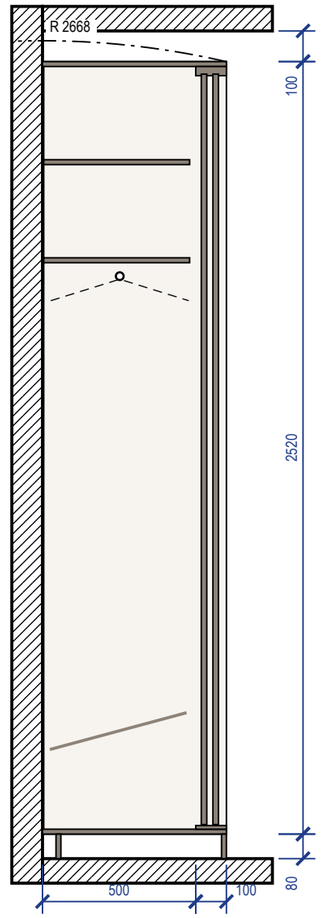


## Разрез 2-2

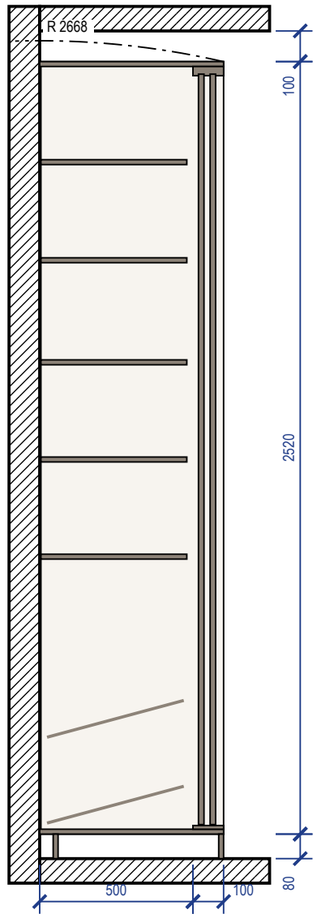


### Примечания

1. Размеры — в мм по чистовой отделке; изделие 1400×600×2600 (Ш×Г×В). Перед раскроем — контрольный замер цеха после чистовой отделки стен, пола и потолка.
2. Корпус — ЛДСП 16 мм, задняя стенка ХДФ 4 мм в паз, цоколь 80 мм на регулируемых опорах; двери купе — ЛДСП 10 мм в алюминиевом профиле, нахлёст 30 мм, ширина двери 699 мм, высота — проём минус 40 мм; цвет — по колерной карте.
3. Кромка: скрытые торцы 0,4 мм, видимые 2 мм (ПВХ/АБС).
4. Номинальные зазоры: дверь купе — боковина 3 мм, фасад ящика — стойка 2 мм; ящики внутри купе — с накладкой 30 мм на стойке со стороны нахлёста дверей.
5. Ящики — направляющие полного выдвижения NL 450 (внутренняя глубина 496 мм ≥ NL + 3); присадка по 32-й системе — выполняет цех.
6. Зазор до потолка 100 мм — закрыть планкой в цвет корпуса при монтаже.
7. Подъём корпуса: диагональ боковины $\sqrt{(2600^2 + 600^2)} = 2668$ мм < 2700 мм до потолка — корпус собирается лёжа и поднимается поворотом.
8. Крепление к стене от опрокидывания — уголки 2 шт. к несущему основанию (монтажная схема шкафов).

## 3D орто

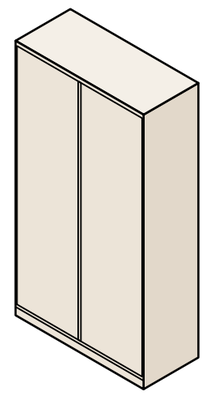

| | | | | | |
|---|---|---|---|---|---|
| | | | | | Проект: Дом 331 м² |
| | Лист | № док. | Подпись | Дата | Шкаф-купе М_24 |
| Дизайнер | Кырлан А.С. | | | 19.10.26 | |

| Стадия | Лист | Листов |
|---|---|---|
| П | Д_3 | 156 |

выпуск 18.10.2026 № 8cd922c868 · стр. 146 из 156

Правка к этому листу

## Общий вид

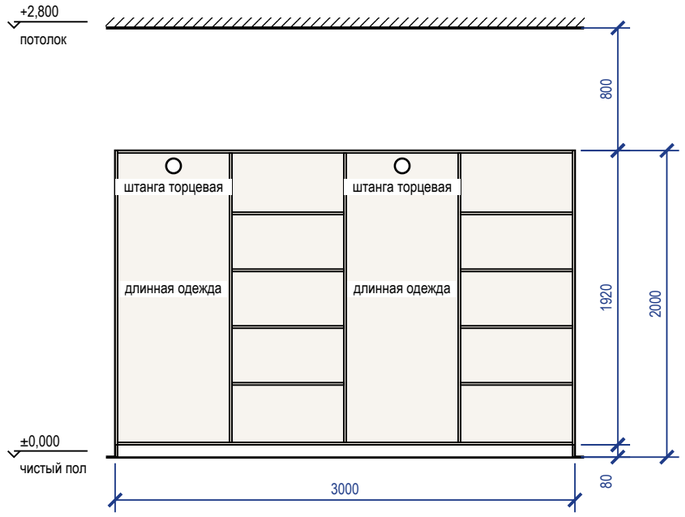


## Наполнение, размеры в свету

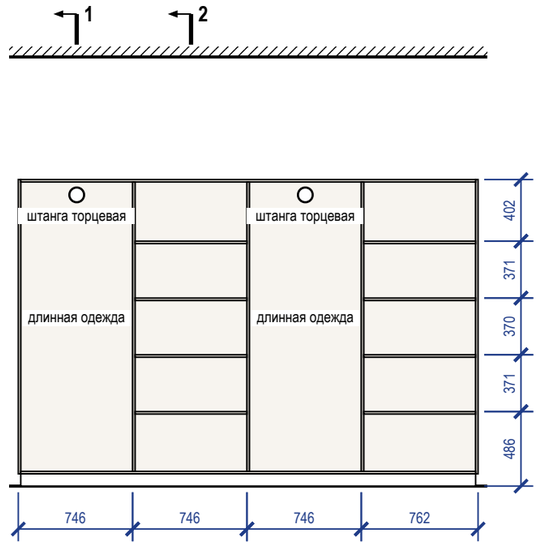


## Разрез 1-1

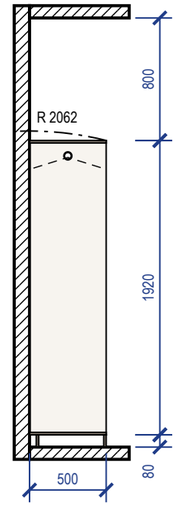


## Разрез 2-2

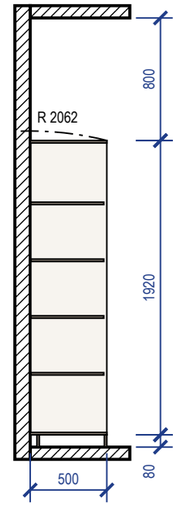


## Примечания

1. Размеры — в мм по чистовой отделке; изделие 3000×500×2000 (Ш×Г×В). Перед раскроем — контрольный замер цеха после чистовой отделки стен, пола и потолка.
2. Корпус — ЛДСП 16 мм, задняя стенка ХДФ 4 мм в паз, цоколь 80 мм на регулируемых опорах; открытая система без фасадов, ящики с фасадами.
3. Кромка: скрытые торцы 0,4 мм, видимые 2 мм (ПВХ/АБС).
4. Номинальные зазоры: между фасадами ящиков 3 мм, фасад ящика — стойка 2 мм.
5. Ящики — направляющие полного выдвижения NL 450 (внутренняя глубина 496 мм ≥ NL + 3); присадка по 32-й системе — выполняет цех.
6. Зазор до потолка 800 мм.
7. Подъём корпуса: диагональ боковины $\sqrt{(2000^2 + 500^2)} = 2062$ мм < 2800 мм до потолка — корпус собирается лёжа и поднимается поворотом.
8. Крепление к стене от опрокидывания: true; основание стены и шаг анкеров — монтажная схема шкафов.

## 3D орто

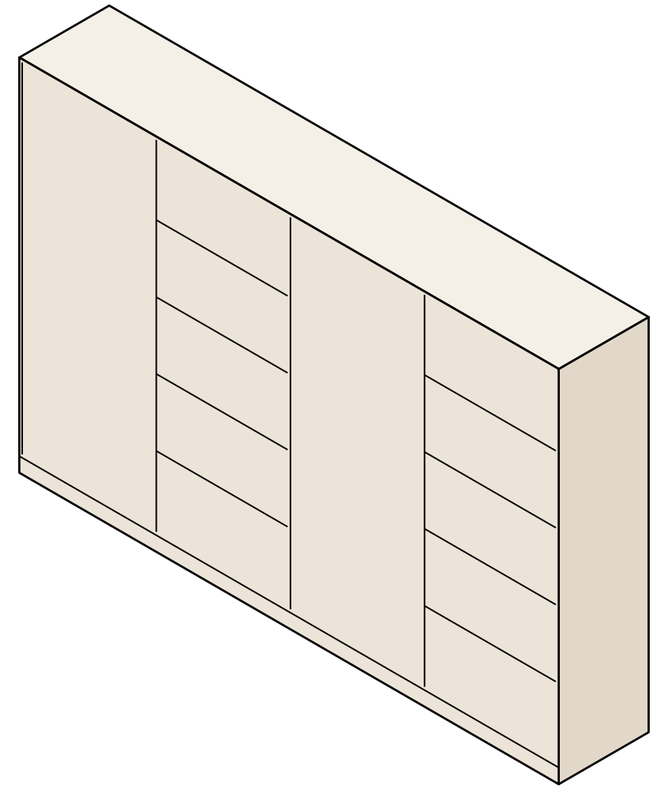

| | | | | | | | |
|---|---|---|---|---|---|---|---|
| | | | | | Проект: Дом 331 м² | | |
| | Лист | № док. | Подпись | Дата | Система хранения M_26 | Стадия | Лист | Листов |
| Дизайнер | Кырлан А.С. | | | 19.10.26 | | П | Д_4 | 156 |

выпуск 18.10.2026 № 8cd922c868 · стр. 147 из 156

Правка к этому листу

## Общий вид

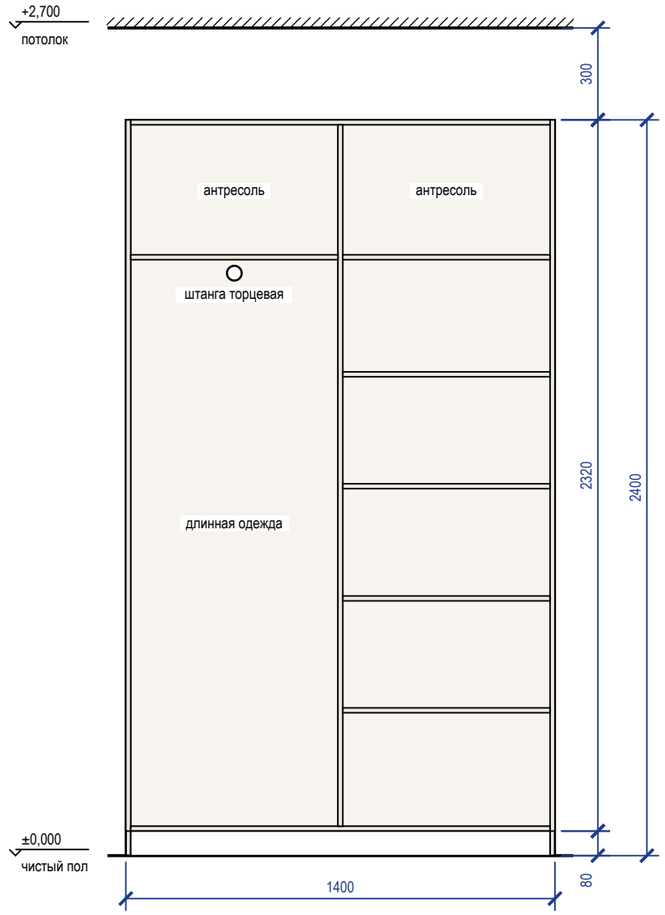


## Наполнение, размеры в свету

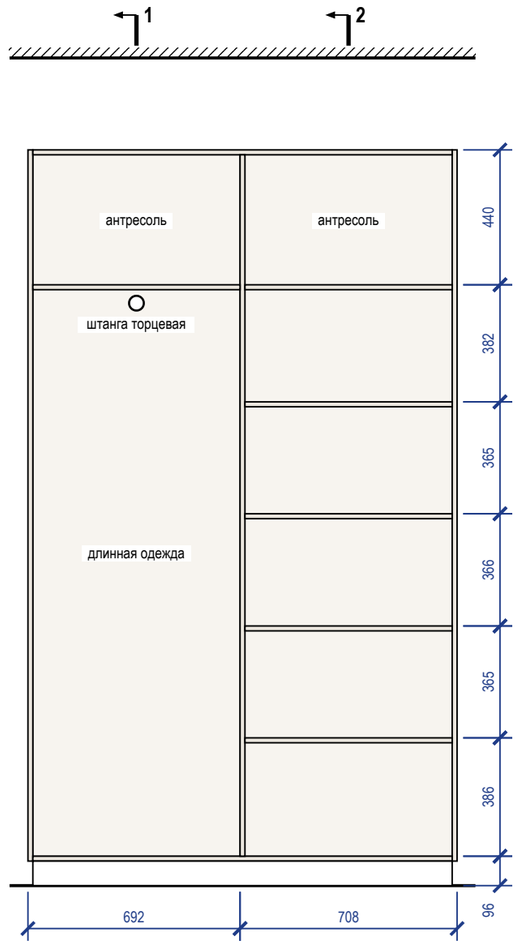


## Разрез 1-1

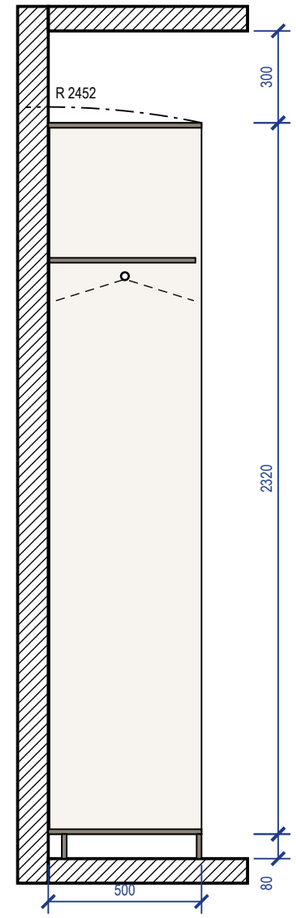


## Разрез 2-2

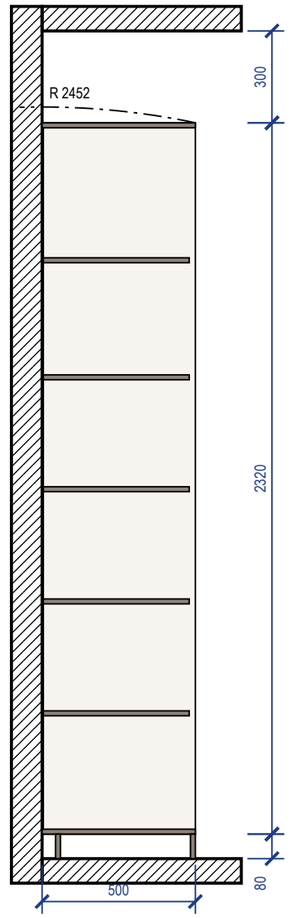


### Примечания

1. Размеры — в мм по чистовой отделке; изделие 1400×500×2400 (Ш×Г×В). Перед раскроем — контрольный замер цеха после чистовой отделки стен, пола и потолка.
2. Корпус — ЛДСП 16 мм, задняя стенка ХДФ 4 мм в паз, цоколь 80 мм на регулируемых опорах; открытая система без фасадов, ящики с фасадами.
3. Кромка: скрытые торцы 0,4 мм, видимые 2 мм (ПВХ/АБС).
4. Номинальные зазоры: между фасадами ящиков 3 мм, фасад ящика — стойка 2 мм.
5. Ящики — направляющие полного выдвижения NL 450 (внутренняя глубина 496 мм ≥ NL + 3); присадка по 32-й системе — выполняет цех.
6. Зазор до потолка 300 мм.
7. Подъём корпуса: диагональ боковины $\sqrt{(2400^2 + 500^2)} = 2452$ мм < 2700 мм до потолка — корпус собирается лёжа и поднимается поворотом.
8. Крепление к стене от опрокидывания — уголки 2 шт. к несущему основанию (монтажная схема шкафов).

## 3D орто

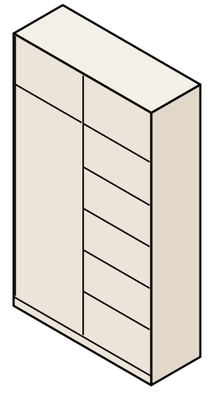

| | | | | | |
|---|---|---|---|---|---|
| | | | | | Проект: Дом 331 м² |
| | Лист | № док. | Подпись | Дата | Система хранения M_43 |
| Дизайнер | Кырлан А.С. | | | 19.10.26 | |

| Стадия | Лист | Листов |
|---|---|---|
| П | Д_5 | 156 |

Правка к этому листу

## Вид с фасадами

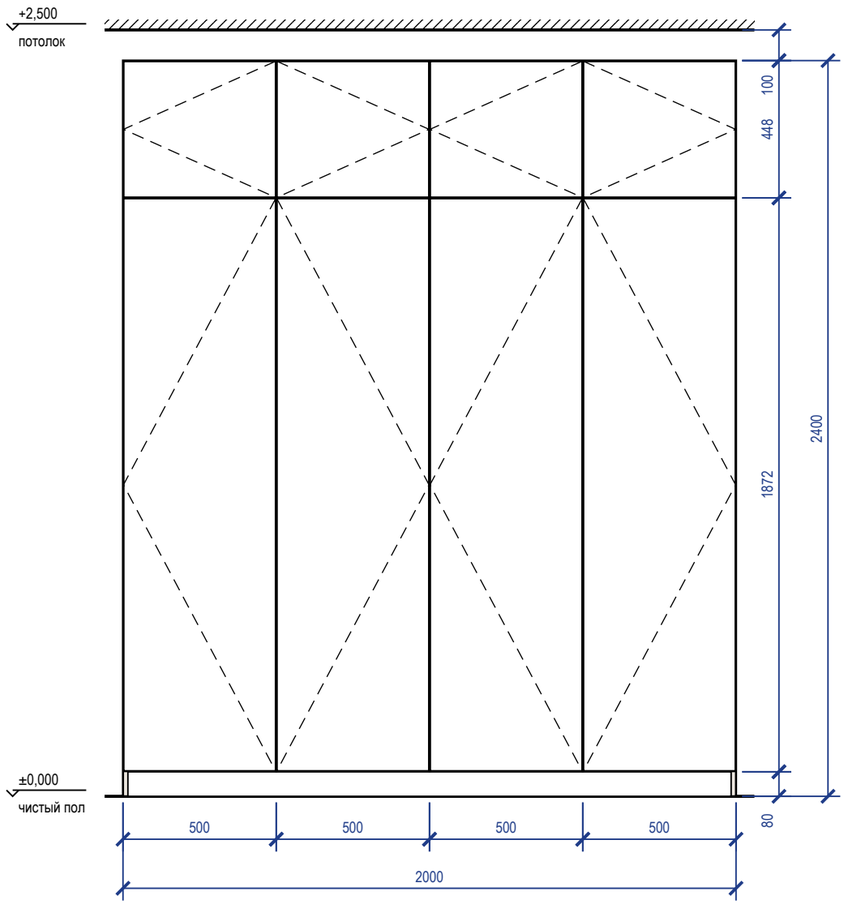


## Вид без фасадов

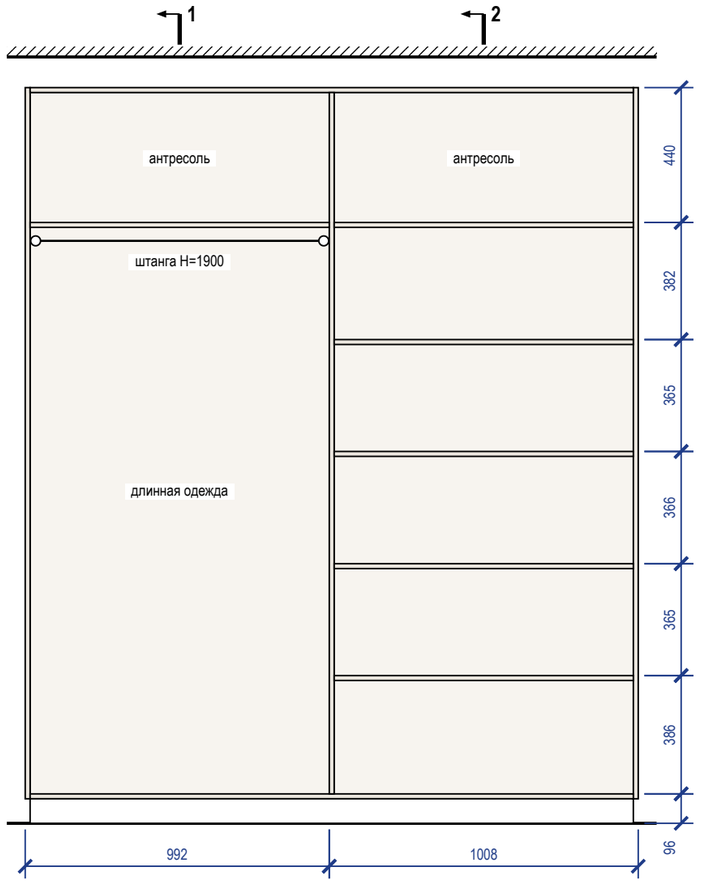


## Разрез 1-1

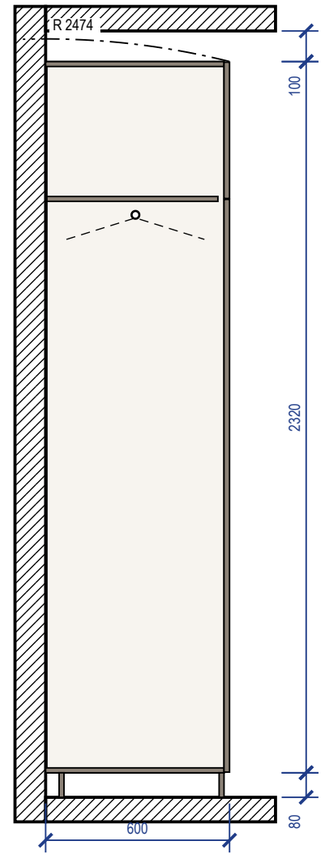


## Разрез 2-2

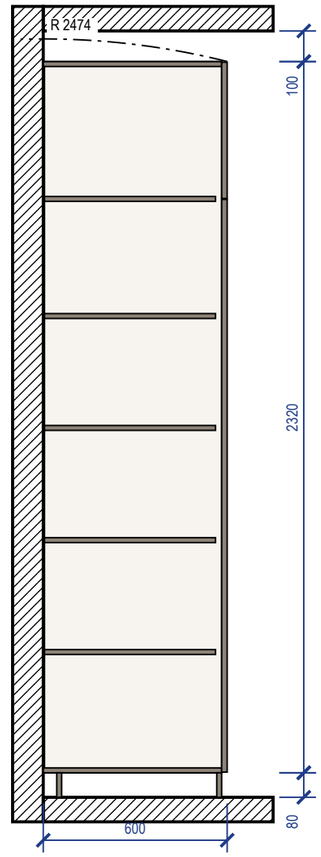


### Примечания

1. Размеры — в мм по чистовой отделке; изделие 2000×600×2400 (Ш×Г×В). Перед раскроем — контрольный замер цеха после чистовой отделки стен, пола и потолка.
2. Корпус — ЛДСП 16 мм, задняя стенка ХДФ 4 мм в паз, цоколь 80 мм на регулируемых опорах; фасады — МДФ, эмаль матовая 18 мм накладные, цвет — по колерной карте; петли с доводчиком: фасад 1869 мм — 4 петли, фасад 445 мм — 2 петли.
3. Кромка: скрытые торцы 0,4 мм, видимые 2 мм (ПВХ/АБС).
4. Номинальные зазоры: между фасадами 3 мм, фасад — стена и фасад — потолок не менее 3 мм, фасад ящика — стойка 2 мм.
5. Ящики — направляющие полного выдвижения NL 550 (внутренняя глубина 578 мм ≥ NL + 3); присадка по 32-й системе — выполняет цех.
6. Зазор до потолка 100 мм — закрыть планкой в цвет корпуса при монтаже.
7. Подъём корпуса: диагональ боковины $\sqrt{(2400^2 + 600^2)} = 2474$ мм < 2500 мм до потолка — корпус собирается лёжа и поднимается поворотом.
8. Крепление к стене от опрокидывания — уголки 2 шт. к несущему основанию (монтажная схема шкафов).

## 3D орто

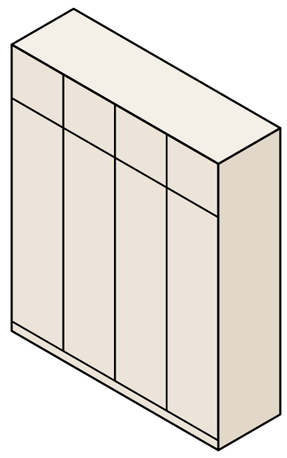

| | | | | | | | |
|---|---|---|---|---|---|---|---|
| | | | | | Проект: Дом 331 м² | | |
| | Лист | № док. | Подпись | Дата | Шкаф распашной М_46 | Стадия | Лист | Листов |
| Дизайнер | Кырлан А.С. | | | 19.10.26 | | П | Д_6 | 156 |

выпуск 18.10.2026 № 8cd922c868 · стр. 149 из 156

Правка к этому листу

## Общий вид

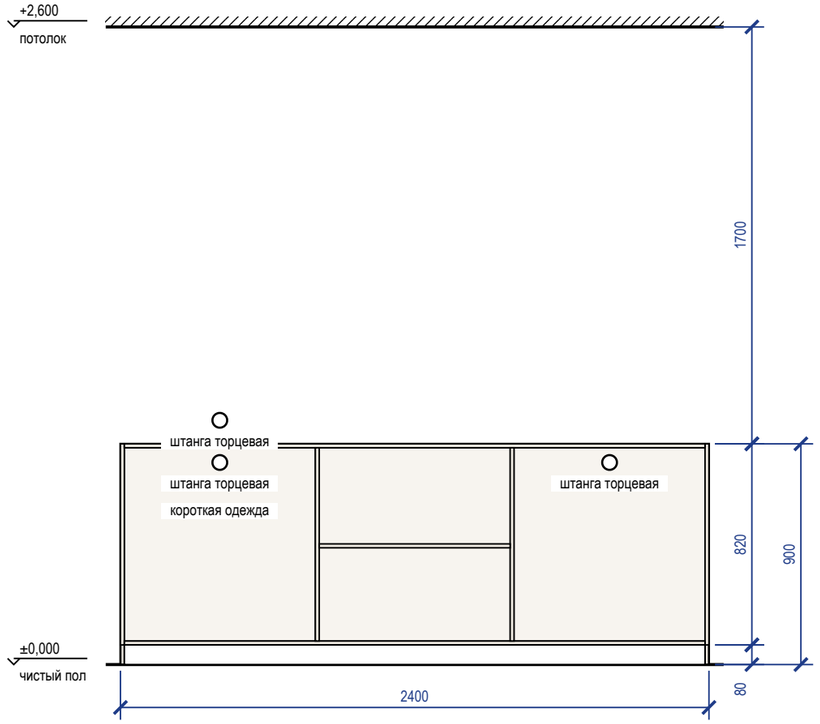


## Наполнение, размеры в свету

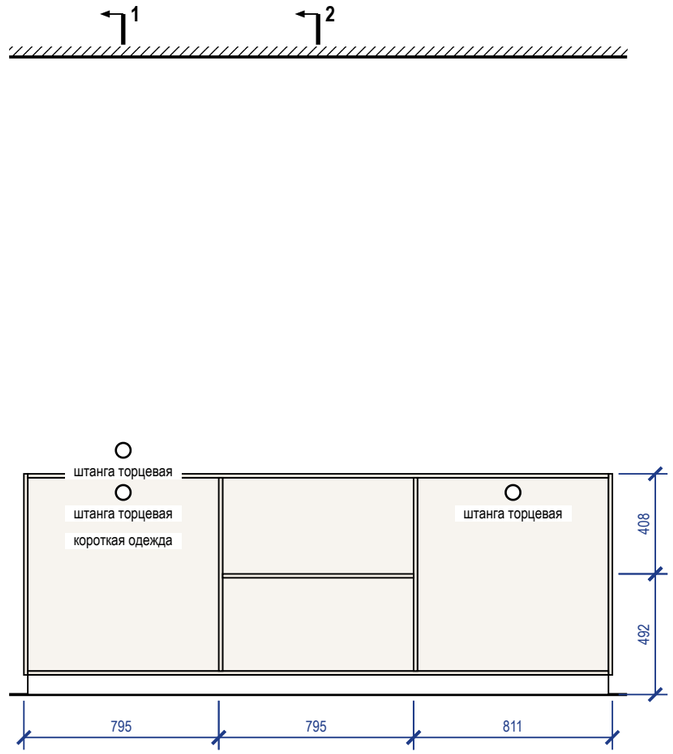


## Разрез 1-1

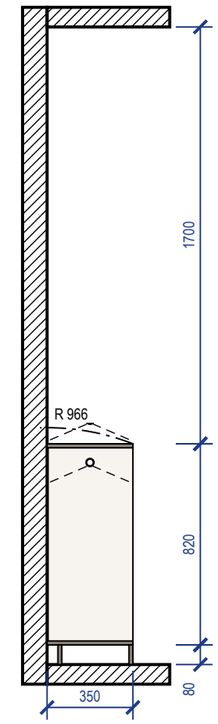


## Разрез 2-2

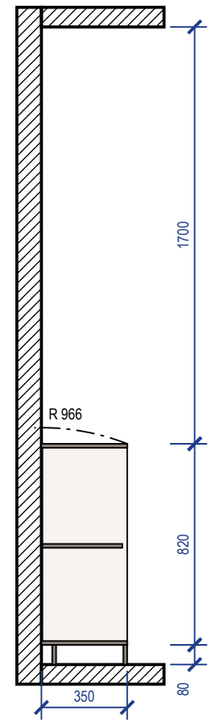


### Примечания

1. Размеры — в мм по чистовой отделке; изделие 2400×350×900 (Ш×Г×В). Перед раскроем — контрольный замер цеха после чистовой отделки стен, пола и потолка.
2. Корпус — ЛДСП 16 мм, задняя стенка ХДФ 4 мм в паз, цоколь 80 мм на регулируемых опорах; открытая система без фасадов, ящики с фасадами.
3. Кромка: скрытые торцы 0,4 мм, видимые 2 мм (ПВХ/АБС).
4. Номинальные зазоры: между фасадами ящиков 3 мм, фасад ящика — стойка 2 мм.
5. Ящики — направляющие полного выдвижения NL 300 (внутренняя глубина 346 мм ≥ NL + 3); присадка по 32-й системе — выполняет цех.
6. Зазор до потолка 1700 мм.
7. Подъём корпуса: диагональ боковины $\sqrt{(900^2 + 350^2)} = 966$ мм < 2600 мм до потолка — корпус собирается лёжа и поднимается поворотом.
8. Крепление к стене от опрокидывания: true; основание стены и шаг анкеров — монтажная схема шкафов.

## 3D орто

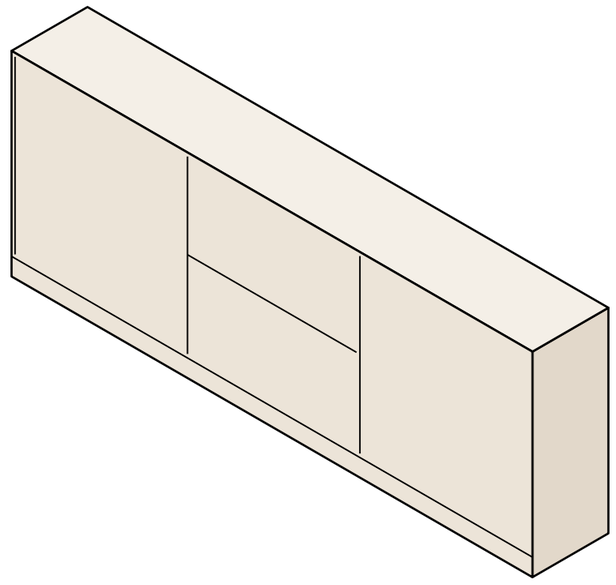

| | | | | | |
|---|---|---|---|---|---|
| | | | | | Проект: Дом 331 м² |
| | Лист | № док. | Подпись | Дата | |
| Дизайнер | Кырлан А.С. | | | 19.10.26 | Система хранения M_49 |

| Стадия | Лист | Листов |
|---|---|---|
| П | Д_7 | 156 |

выпуск 18.10.2026 № 8cd922c868 · стр. 150 из 156

Правка к этому листу

## Вид с фасадами

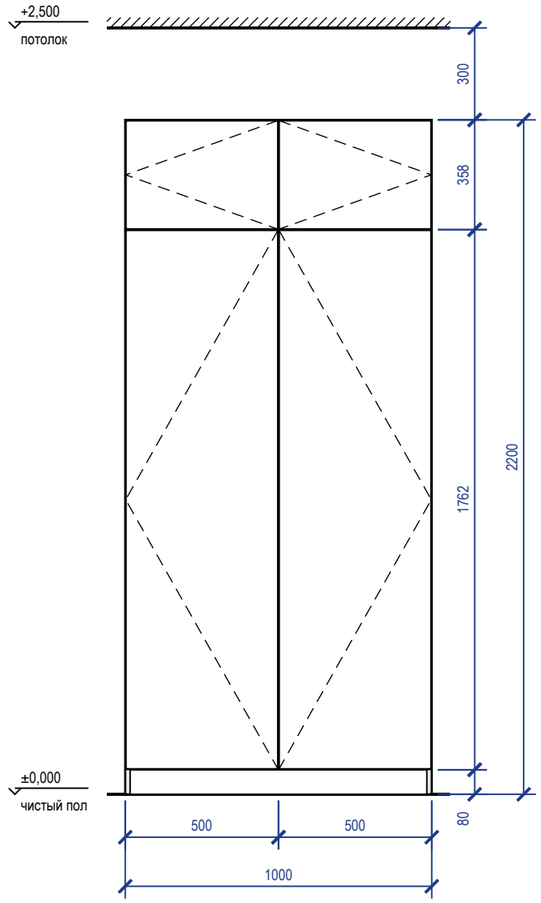


## Вид без фасадов

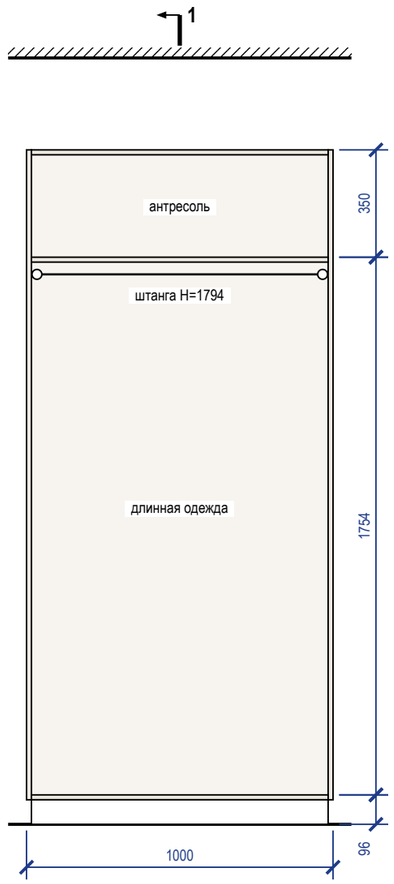


## Разрез 1-1

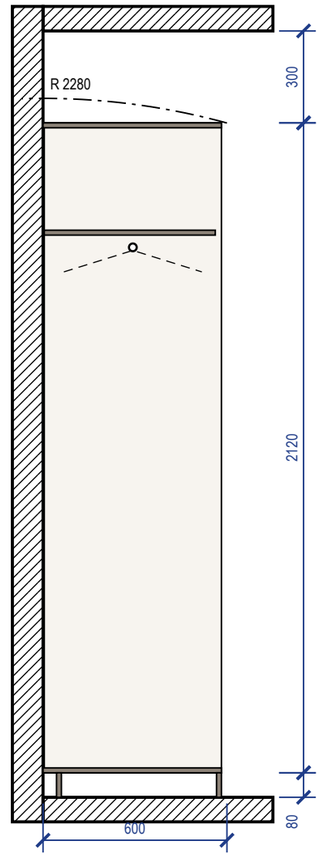


### Примечания

1. Размеры — в мм по чистовой отделке; изделие 1000×600×2200 (Ш×Г×В). Перед раскроем — контрольный замер цеха после чистовой отделки стен, пола и потолка.
2. Корпус — ЛДСП 16 мм, задняя стенка ХДФ 4 мм в паз, цоколь 80 мм на регулируемых опорах; фасады — МДФ, эмаль матовая 18 мм накладные, цвет — по колерной карте; петли с доводчиком: фасад 1759 мм — 4 петли, фасад 355 мм — 2 петли.
3. Кромка: скрытые торцы 0,4 мм, видимые 2 мм (ПВХ/АБС).
4. Номинальные зазоры: между фасадами 3 мм, фасад — стена и фасад — потолок не менее 3 мм, фасад ящика — стойка 2 мм.
5. Ящики — направляющие полного выдвижения NL 550 (внутренняя глубина 578 мм ≥ NL + 3); присадка по 32-й системе — выполняет цех.
6. Зазор до потолка 300 мм.
7. Подъём корпуса: диагональ боковины $\sqrt{(2200^2 + 600^2)} = 2280$ мм < 2500 мм до потолка — корпус собирается лёжа и поднимается поворотом.
8. Крепление к стене от опрокидывания — уголки 2 шт. к несущему основанию (монтажная схема шкафов).

## 3D орто

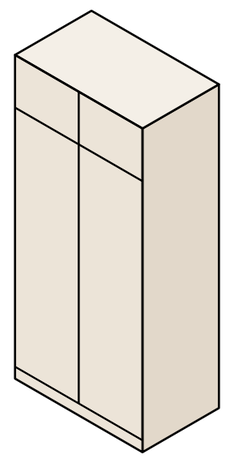

| | | | | | | | |
|---|---|---|---|---|---|---|---|
| | | | | | Проект: Дом 331 м² | | |
| | Лист | № док. | Подпись | Дата | Шкаф распашной М_53 | Стадия | Лист | Листов |
| Дизайнер | Кырлан А.С. | | | 19.10.26 | | П | Д_8 | 156 |

выпуск 18.10.2026 № 8cd922c868 · стр. 151 из 156

Правка к этому листу

## Вид с фасадами

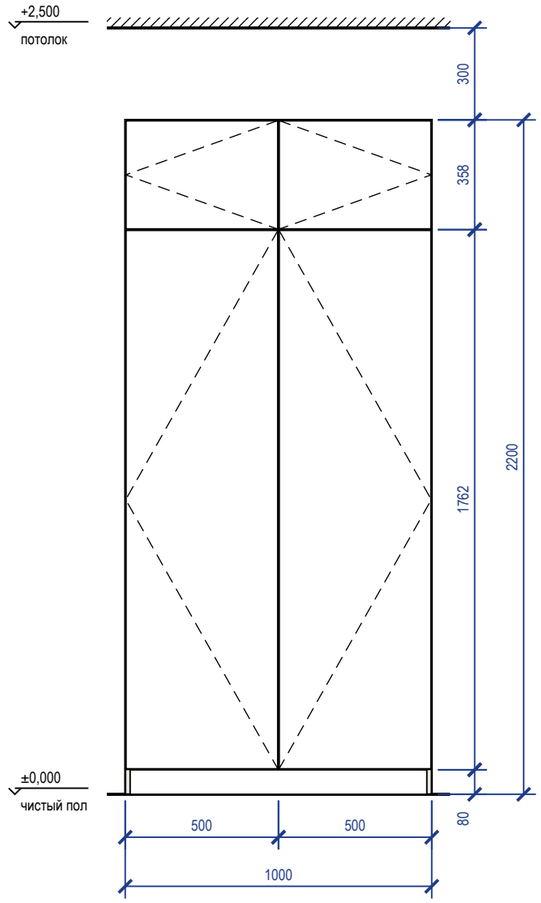


## Вид без фасадов

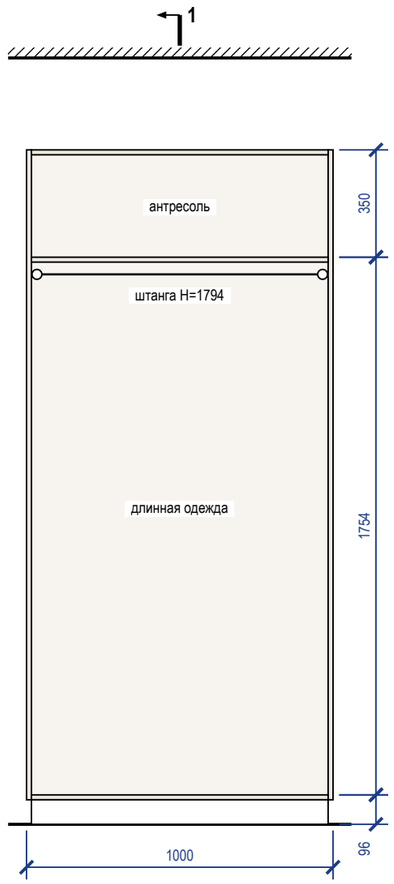


## Разрез 1-1

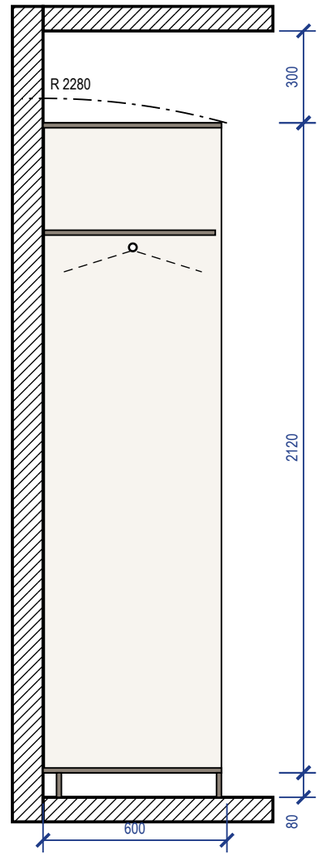


### Примечания

1. Размеры — в мм по чистовой отделке; изделие 1000×600×2200 (Ш×Г×В). Перед раскроем — контрольный замер цеха после чистовой отделки стен, пола и потолка.
2. Корпус — ЛДСП 16 мм, задняя стенка ХДФ 4 мм в паз, цоколь 80 мм на регулируемых опорах; фасады — МДФ, эмаль матовая 18 мм накладные, цвет — по колерной карте; петли с доводчиком: фасад 1759 мм — 4 петли, фасад 355 мм — 2 петли.
3. Кромка: скрытые торцы 0,4 мм, видимые 2 мм (ПВХ/АБС).
4. Номинальные зазоры: между фасадами 3 мм, фасад — стена и фасад — потолок не менее 3 мм, фасад ящика — стойка 2 мм.
5. Ящики — направляющие полного выдвижения NL 550 (внутренняя глубина 578 мм ≥ NL + 3); присадка по 32-й системе — выполняет цех.
6. Зазор до потолка 300 мм.
7. Подъём корпуса: диагональ боковины $\sqrt{(2200^2 + 600^2)} = 2280$ мм < 2500 мм до потолка — корпус собирается лёжа и поднимается поворотом.
8. Крепление к стене от опрокидывания — уголки 2 шт. к несущему основанию (монтажная схема шкафов).

## 3D орто

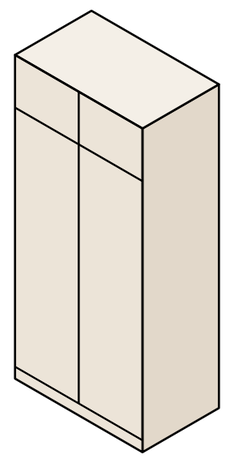

| | | | | | | | |
|---|---|---|---|---|---|---|---|
| | | | | | Проект: Дом 331 м² | | |
| | Лист | № док. | Подпись | Дата | Шкаф распашной М_56 | Стадия | Лист | Листов |
| Дизайнер | Кырлан А.С. | | | 19.10.26 | | П | Д_9 | 156 |

выпуск 18.10.2026 № 8cd922c868 · стр. 152 из 156

Правка к этому листу

## Вид с фасадами

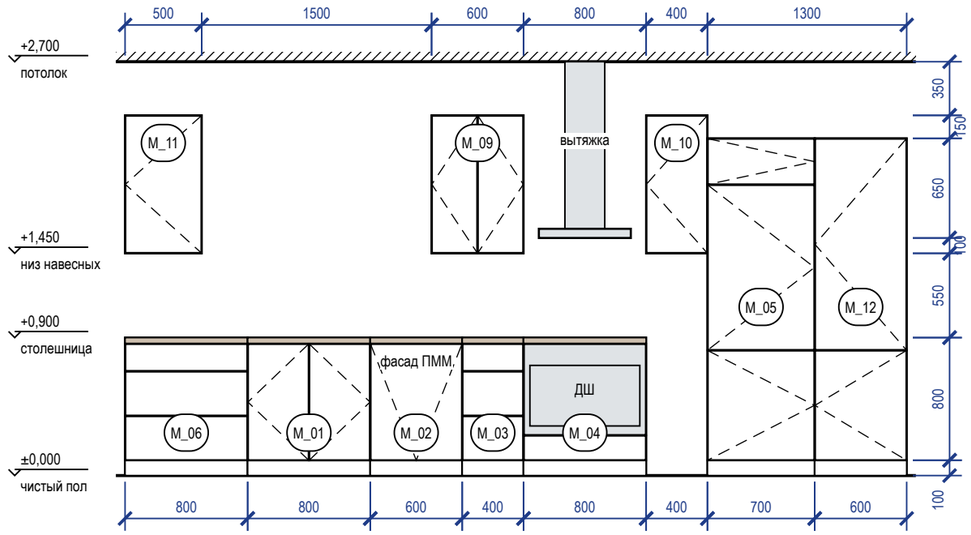


## Вид без фасадов (наполнение, выводы)

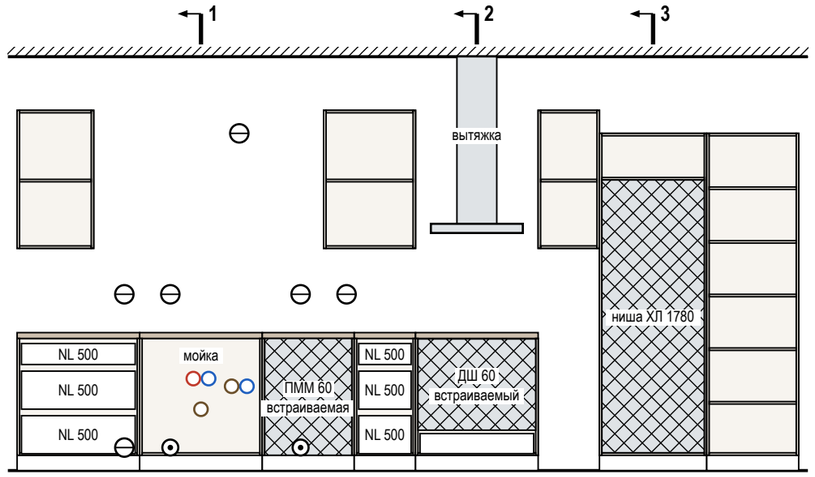


## Разрез 1-1

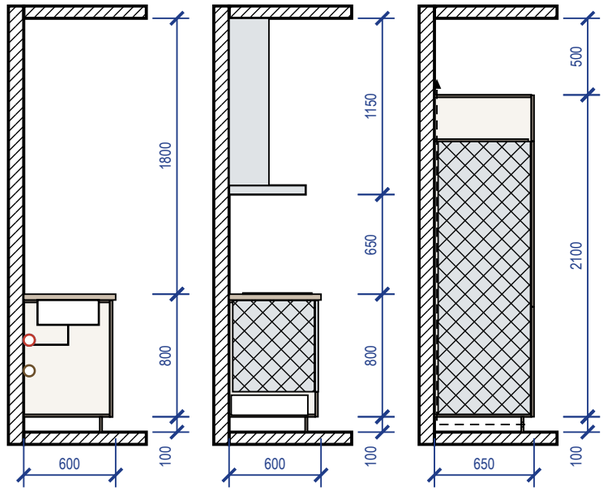


## Разрез 2-2




## Разрез 3-3




## 3D орто

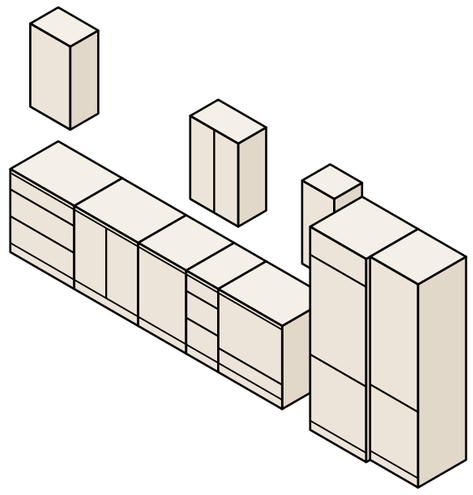

## Примечания

1. Размеры — в мм по чистовой отделке, вид из помещения; марки — как на плане расстановки. Перед раскроем — контрольный замер цеха после фартука и пола.
2. Корпуса — ЛДСП 16 мм, задняя стенка ХДФ 4 мм; фасады — МДФ, эмаль матовая 18 мм, цвет по колерной карте; столешница 38 мм, свес 20 мм; цоколь 100 мм.
3. Кромка: скрытые торцы 0,4 мм, видимые 2 мм. Номинальные зазоры: между фасадами 3 мм, фасад — столешница 3 мм, фасад — стена не менее 3 мм.
4. Ящики полного выдвижения и петли — с доводчиком; присадка по 32-й системе — выполняет цех.
5. Низ вытяжки — не ниже 650 мм над варочной панелью или по паспорту модели; короб воздуховода — до потолка.
6. Ниши техники (холодильник — ориентир 1780 мм) — по монтажным схемам выбранных моделей: решётка в цоколе и канал за пеналом холодильника, зазор за духовым шкафом, фасад ПММ на двери машины.

| | | | | | |
|---|---|---|---|---|---|
| | | | | | Проект: Дом 331 м² |
| | Лист | № док. | Подпись | Дата | Кухня (пом. 1). Развёртка гарнитура |
| Дизайнер | Кырлан А.С. | | | 19.10.26 | |

| Стадия | Лист | Листов |
|---|---|---|
| П | Д_10 | 156 |

выпуск 18.10.2026 № 8cd922c868 · стр. 153 из 156

Правка к этому листу

## Ведомость отделки помещений (форма 1 прил. А ГОСТ 21.501-2018). Лист 1 из 3

| № | Наименование помещения | Потолок | | | Стены и перегородки | | | Низ стен (плинтус) | | | Пол | | Примечание |
|---|---|---|---|---|---|---|---|---|---|---|---|---|---|
| | | Вид отделки | Код цвета | S, м² | Вид отделки | Код цвета | S, м² | Вид отделки | Код цвета | L, м | Вид отделки | S, м² | |
| 1 | Кухня-столовая<br>24,59 м² | ГКЛ по каркасу П113, отм. +2,700; окраска, Tikkurila Luja 7, матовая, 2 слоя, подготовка Q3 | NCS S<br>0804-Y30R | 24,59 | Окраска, Tikkurila Luja 7, полуматовая, 2 слоя, подготовка К3<br>Фартук кухни (стена А): облицовка керамогранитом, аналог: керамогранит матовый, тон F497, 600×600×9 мм, клей C2 TE S1, затирка CG2WA | NCS S<br>0804-Y30R<br>#F1F1EC | 45,02<br>0,93 | Плинтус МДФ h=80 мм, аналог: МДФ под окраску 80×16 мм | NCS S<br>0804-Y30R | 18,3 | Инженерная доска, 1167-4250, 2100×127 мм, на клею; тип 1, отм. ЧП ±0,000 | 24,59 | Н стен 2700 (до потолка); влагостойкая полуматовая окраска (класс мокрого истирания 1 по EN 13300); категория К3 по СП 71.13330.2017, табл. 7.5; по ГКЛ каркаса П113, влагостойкая окраска; Q3 колеруется в код стен, но по эмали на МДФ: сличать отдельным выкрасом на своей подложке (выкрас № 10); плинтус в цвет: стены |
| 2 | Кабинет-гостевая<br>11,92 м² | ГКЛ по каркасу П113, отм. +2,650; +2,700; окраска, Tikkurila Anti-Reflex 2, глубокоматовая, 2 слоя, подготовка Q3 | Little Greene<br>No. 105 | 11,92 | Окраска, Farrow & Ball Modern Emulsion, матовая, 2 слоя, подготовка Q3<br>Акцент — стена А: окраска, Farrow & Ball Modern Emulsion, матовая, 2 слоя, подготовка Q3 | Farrow & Ball<br>No. 226<br>Farrow & Ball<br>No. 298 | 24,74<br>5,53 | Плинтус МДФ h=80 мм, аналог: МДФ под покраску 80×16 | Farrow & Ball<br>No. 226 | 11,7 | Инженерная доска, 1167-4250, 2100×127 мм, на клею; тип 2, отм. ЧП ±0,000 | 11,92 | Н стен 2650 (до потолка); плинтус в цвет: стены |
| 3 | Санузел 1 этажа<br>4,87 м² | ГКЛВ по каркасу П113, отм. +2,600; окраска, Tikkurila Luja 7, матовая, 2 слоя, подготовка Q3 | Little Greene<br>No. 105 | 4,87 | Облицовка плиткой, A8UZ, 600×1200×9 мм, клей C2 TE S1, затирка CG2WA | Atlas Concorde<br>A8UZ | 20,53 | нет | | | Керамогранит, A8UZ, 600×1200×9 мм; тип 3, отм. ЧП −0,015 | 4,87 | Н стен 2615 (до потолка); гидроизоляция обмазочная, 2 слоя, с заведением на стены 200 мм (по пирогу пола); тест проливом и акт скрытых работ |
| 4 | Котельная<br>6,88 м² | Окраска, Tikkurila Anti-Reflex 2, глубокоматовая, 2 слоя, подготовка Q3 | Little Greene<br>No. 105 | 6,88 | Окраска, Farrow & Ball Modern Emulsion, матовая, 2 слоя, подготовка Q3 | Farrow & Ball<br>No. 226 | 26,96 | Плинтус МДФ h=80 мм, аналог: МДФ под покраску 80×16 | Farrow & Ball<br>No. 226 | 9,7 | Керамогранит, A8UZ, 600×1200×9 мм; тип 4, отм. ЧП ±0,000 | 6,88 | Н стен 2800 (до потолка); матовая моющаяся, класс 1 EN 13300 — осознанно вместо полуматовой; плинтус в цвет: стены |
| 5 | Гостиная<br>33,74 м² | ГКЛ по каркасу П113, отм. +2,650; +2,700; окраска, Tikkurila Anti-Reflex 2, глубокоматовая, 2 слоя, подготовка Q3 | NCS S<br>0804-Y30R | 33,74 | Окраска, Tikkurila Optiva 5 Matt, матовая, 2 слоя, подготовка К3<br>Акцент — стена А: окраска, Tikkurila Optiva 5 Matt, матовая, 3 слоя, подготовка К3 | NCS S<br>0804-Y30R<br>Farrow & Ball<br>No. 93 | 33,06<br>13,22 | Плинтус МДФ h=80 мм, аналог: МДФ под окраску 80×16 мм | NCS S<br>0804-Y30R | 18,2 | Инженерная доска, 1167-4250, 2100×127 мм, на клею; тип 5, отм. ЧП ±0,000 | 33,74 | Н стен 2650 (до потолка); колеруется в код стен, но по эмали на МДФ: сличать отдельным выкрасом на своей подложке (выкрас № 10); плинтус в цвет: стены |
| 6 | Холл с лестницей<br>10,02 м² | ГКЛ по каркасу П113, отм. +2,700; окраска, Tikkurila Anti-Reflex 2, глубокоматовая, 2 слоя, подготовка Q3 | Little Greene<br>No. 105 | 10,02 | Окраска, Farrow & Ball Modern Emulsion, матовая, 2 слоя, подготовка Q3 | Farrow & Ball<br>No. 226 | 22,29 | Плинтус МДФ h=80 мм, аналог: МДФ под покраску 80×16 | Farrow & Ball<br>No. 226 | 7,0 | Инженерная доска, 1167-4250, 2100×127 мм, на клею; тип 2, отм. ЧП ±0,000 | 10,02 | Н стен 2700 (до потолка); матовая моющаяся, класс 1 EN 13300 — осознанно вместо полуматовой; плинтус в цвет: стены |
| 7 | Кладовая<br>5,99 м² | Окраска, Tikkurila Anti-Reflex 2, глубокоматовая, 2 слоя, подготовка Q3 | Little Greene<br>No. 105 | 5,99 | Окраска, Tikkurila Harmony, матовая, 2 слоя, подготовка Q3 | Little Greene<br>No. 105 | 23,28 | Плинтус МДФ h=80 мм, аналог: МДФ под покраску 80×16 | Little Greene<br>No. 105 | 7,8 | Инженерная доска, 1167-4250, 2100×127 мм, на клею; тип 2, отм. ЧП ±0,000 | 5,99 | Н стен 2800 (до потолка); плинтус в цвет: стены |
| 8 | Прихожая<br>12,46 м² | ГКЛ по каркасу П113, отм. +2,700; окраска, Tikkurila Anti-Reflex 2, глубокоматовая, 2 слоя, подготовка Q3 | Little Greene<br>No. 105 | 12,46 | Окраска, Farrow & Ball Modern Emulsion, матовая, 2 слоя, подготовка Q3 | Farrow & Ball<br>No. 226 | 38,99 | Плинтус МДФ h=80 мм, аналог: МДФ под покраску 80×16 | Farrow & Ball<br>No. 226 | 13,6 | Керамогранит, A8UZ, 600×1200×9 мм; тип 4, отм. ЧП ±0,000 | 12,46 | Н стен 2700 (до потолка); матовая моющаяся, класс 1 EN 13300 — осознанно вместо полуматовой; плинтус в цвет: стены |
| 9 | Тамбур<br>3,49 м² | Окраска, Tikkurila Anti-Reflex 2, глубокоматовая, 2 слоя, подготовка Q3 | Little Greene<br>No. 105 | 3,49 | Окраска, Farrow & Ball Modern Emulsion, матовая, 2 слоя, подготовка Q3 | Farrow & Ball<br>No. 226 | 17,07 | Плинтус МДФ h=80 мм, аналог: МДФ под покраску 80×16 | Farrow & Ball<br>No. 226 | 5,6 | Керамогранит, A8UZ, 600×1200×9 мм; тип 4, отм. ЧП ±0,000 | 3,49 | Н стен 2800 (до потолка); матовая моющаяся, класс 1 EN 13300 — осознанно вместо полуматовой; плинтус в цвет: стены |

### Примечания

1. Ведомость продолжена на листе 2 из 3; итоги, сводка площадей и примечания — на последнем листе ведомости.

| | | | | | |
|---|---|---|---|---|---|
| | | | | | Проект: Дом 331 м² |
| | Лист | № док. | Подпись | Дата | Ведомость отделки помещений. Лист 1 из 3 |
| Дизайнер | Кырлан А.С. | | | 19.10.26 | |

| Стадия | Лист | Листов |
|---|---|---|
| П | С1 | 156 |

выпуск 18.10.2026 № 8cd922c868 · стр. 154 из 156

Правка к этому листу

| Поз. | Наименование и техническая характеристика | Тип, марка, обозначение документа | Код продукции | Поставщик | Ед. изм. | Кол. | Образец | Примечание |
|---|---|---|---|---|---|---|---|---|
| | **Лакокрасочные материалы** | | | | | | | |
| 1 | Краска интерьерная водно-дисперсионная акриловая для стен, полуматовая, класс мокрого истирания 1 по EN 13300, база A; цвет NCS S 0804-Y30R «S 0804-Y30R», колеровка машинная | Tikkurila Luja 7 | | Tikkurila | л | 30,6 | | поз. К1 колерной карты; пом. 1, 11, 12; S = 113,4 м² × 2 сл. × 0,12 л/м² = 27,2 л, +10 % и 0,5 л на подкраску → ≥ 30,4 л; тара 3 × 9 л + 1 × 2,7 л + 1 × 0,9 л |
| 2 | Краска интерьерная водно-дисперсионная акриловая для потолков, матовая, класс мокрого истирания 1 по EN 13300, база A; цвет NCS S 0804-Y30R «S 0804-Y30R», колеровка машинная | Tikkurila Luja 7 | | Tikkurila | л | 14,4 | | поз. К2 колерной карты; пом. 1, 11, 12; S = 49,8 м² × 2 сл. × 0,12 л/м² = 12,0 л, +10 % и 0,5 л на подкраску → ≥ 13,6 л; тара 1 × 9 л + 2 × 2,7 л |
| 3 | Краска интерьерная водно-дисперсионная акриловая для стен, матовая, класс мокрого истирания 1 по EN 13300, база A; цвет Farrow & Ball No. 226 «Joa's White», колеровка машинная | Farrow & Ball Modern Emulsion | | Farrow & Ball | л | 87,5 | | поз. К4 колерной карты; пом. 2, 4, 6, 8, 9, 10, 13, 16, 17, 18, 19; S = 325,4 м² × 2 сл. × 0,12 л/м² = 78,1 л, +10 % и 0,5 л на подкраску → ≥ 86,4 л; тара 17 × 5 л + 1 × 2,5 л |
| 4 | Краска интерьерная водно-дисперсионная акриловая для акцентных стен, матовая, класс мокрого истирания 1 по EN 13300, база C; цвет Farrow & Ball No. 298 «Bancha», колеровка машинная | Farrow & Ball Modern Emulsion | | Farrow & Ball | л | 2,5 | | поз. К5 колерной карты; пом. 2; S = 5,5 м² × 2 сл. × 0,12 л/м² = 1,3 л, +10 % и 0,5 л на подкраску → ≥ 2,0 л; тара 1 × 2,5 л |
| 5 | Краска интерьерная водно-дисперсионная акриловая для потолков, глубокоматовая, класс мокрого истирания 2 по EN 13300, база A; цвет Little Greene No. 105 «Slaked Lime», колеровка машинная | Tikkurila Anti-Reflex 2 | | Tikkurila | л | 54,9 | | поз. К6 колерной карты; пом. 2, 4, 6, 7, 8, 9, 10, 13, 14, 16, 17, 18, 19; S = 202,9 м² × 2 сл. × 0,12 л/м² = 48,7 л, +10 % и 0,5 л на подкраску → ≥ 54,1 л; тара 6 × 9 л + 1 × 0,9 л |
| 6 | Краска интерьерная водно-дисперсионная акриловая для потолков, матовая, класс мокрого истирания 1 по EN 13300, база A; цвет Little Greene No. 105 «Slaked Lime», колеровка машинная | Tikkurila Luja 7 | | Tikkurila | л | 6,3 | | поз. К9 колерной карты; пом. 3, 15, 20; S = 20,9 м² × 2 сл. × 0,12 л/м² = 5,0 л, +10 % и 0,5 л на подкраску → ≥ 6,0 л; тара 2 × 2,7 л + 1 × 0,9 л |
| 7 | Краска интерьерная водно-дисперсионная акриловая для стен, матовая, класс мокрого истирания 2 по EN 13300, база A; цвет NCS S 0804-Y30R «S 0804-Y30R», колеровка машинная | Tikkurila Optiva 5 Matt | | Tikkurila | л | 9,9 | | поз. К10 колерной карты; пом. 5; S = 33,1 м² × 2 сл. × 0,12 л/м² = 7,9 л, +10 % и 0,5 л на подкраску → ≥ 9,2 л; тара 1 × 9 л + 1 × 0,9 л |
| 8 | Краска интерьерная водно-дисперсионная акриловая для акцентных стен, матовая, класс мокрого истирания 2 по EN 13300, база C; цвет Farrow & Ball No. 93 «Studio Green — почти чёрный зелёный», колеровка машинная | Tikkurila Optiva 5 Matt | | Tikkurila | л | 7,5 | | поз. К11 колерной карты; пом. 5; S = 13,2 м² × 3 сл. × 0,12 л/м² = 4,8 л, +10 % и 0,5 л на подкраску → ≥ 5,7 л; тара 1 × 5 л + 1 × 2,5 л |
| 9 | Краска интерьерная водно-дисперсионная акриловая для потолков, глубокоматовая, класс мокрого истирания 2 по EN 13300, база A; цвет NCS S 0804-Y30R «S 0804-Y30R», колеровка машинная | Tikkurila Anti-Reflex 2 | | Tikkurila | л | 9,9 | | поз. К12 колерной карты; пом. 5; S = 33,7 м² × 2 сл. × 0,12 л/м² = 8,1 л, +10 % и 0,5 л на подкраску → ≥ 9,4 л; тара 1 × 9 л + 1 × 0,9 л |
| 10 | Краска интерьерная водно-дисперсионная акриловая для стен, матовая, класс мокрого истирания 1 по EN 13300, база A; цвет Little Greene No. 105 «Slaked Lime», колеровка машинная | Tikkurila Harmony | | Tikkurila | л | 11,7 | | поз. К13 колерной карты; пом. 7, 14; S = 42,0 м² × 2 сл. × 0,12 л/м² = 10,1 л, +10 % и 0,5 л на подкраску → ≥ 11,6 л; тара 1 × 9 л + 1 × 2,7 л |
| 11 | Краска интерьерная водно-дисперсионная акриловая для акцентных стен, матовая, класс мокрого истирания 1 по EN 13300, база C; цвет NCS S 7020-G10Y «Хвойный тёмно-зелёный», колеровка машинная | Farrow & Ball Modern Emulsion | | Farrow & Ball | л | 5 | | поз. К15 колерной карты; пом. 13; S = 7,6 м² × 2 сл. × 0,12 л/м² = 1,8 л, +10 % и 0,5 л на подкраску → ≥ 2,5 л; тара 1 × 5 л |
| 12 | Краска интерьерная водно-дисперсионная акриловая для акцентных стен, матовая, класс мокрого истирания 1 по EN 13300, база C; цвет Farrow & Ball No. 64 «Red Earth», колеровка машинная | Farrow & Ball Modern Emulsion | | Farrow & Ball | л | 2,5 | | поз. К16 колерной карты; пом. 16; S = 7,3 м² × 2 сл. × 0,12 л/м² = 1,8 л, +10 % и 0,5 л на подкраску → ≥ 2,4 л; тара 1 × 2,5 л |
| 13 | Краска интерьерная водно-дисперсионная акриловая для акцентных стен, матовая, класс мокрого истирания 1 по EN 13300, база C; цвет NCS S 3020-G30Y «S 3020-G30Y», колеровка машинная | Farrow & Ball Modern Emulsion | | Farrow & Ball | л | 5 | | поз. К17 колерной карты; пом. 18; S = 12,3 м² × 2 сл. × 0,12 л/м² = 3,0 л, +10 % и 0,5 л на подкраску → ≥ 3,8 л; тара 1 × 5 л |
| 14 | Краска интерьерная водно-дисперсионная акриловая для акцентных стен, матовая, класс мокрого истирания 1 по EN 13300, база C; цвет NCS S 3040-Y70R «S 3040-Y70R», колеровка машинная | Farrow & Ball Modern Emulsion | | Farrow & Ball | л | 5 | | поз. К19 колерной карты; пом. 19; S = 14,8 м² × 2 сл. × 0,12 л/м² = 3,6 л, +10 % и 0,5 л на подкраску → ≥ 4,4 л; тара 1 × 5 л |
| 15 | Акрилово-уретановая эмаль на водной основе, полуглянцевая в цвет NCS S 0804-Y30R «S 0804-Y30R» — окраска плинтуса | аналог по характеристикам | | | л | 1 | | поз. К3; пом. 1, 5; L = 36,5 м, S = 3,5 м² × 2 сл. × 0,12 л/м² + 10 %; продукт подобрать в веере NCS |
| 16 | Краска для МДФ и дерева в цвет Farrow & Ball No. 226 «Joa's White» — окраска плинтуса; блеск не ниже блеска стен | марка не задана | | | л | 3,2 | | поз. К7, К18; пом. 2, 4, 6, 8, 9, 13, 16, 17, 18, 19; L = 127,7 м, S = 11,9 м² × 2 сл. × 0,12 л/м² + 10 %; продукт подобрать в веере Farrow & Ball |
| 17 | Краска для МДФ и дерева в цвет Little Greene No. 105 «Slaked Lime» — окраска плинтуса; блеск не ниже блеска стен | марка не задана | | | л | 0,5 | | поз. К14; пом. 7, 14; L = 16,8 м, S = 1,6 м² × 2 сл. × 0,12 л/м² + 10 %; продукт подобрать в веере Little Greene |
| 18 | Грунтовка акриловая под окраску стен и потолков — из системы производителя краски | по системе краски | | | м² | 882 | | площадь окраски стен, акцентов и потолков; 1 слой перед окраской; расход — по ТУ грунтовки |

| | | | | | |
|---|---|---|---|---|---|
| | Лист | № док. | Подпись | Дата | |
| Дизайнер | Кырлан А.С. | | | 19.10.26 | |

Проект: Дом 331 м²

Спецификация отделочных материалов

| Стадия | Лист | Листов |
|---|---|---|
| П | С2 | 156 |

Правка к этому листу

## 1 Порог 15 мм: мокрая зона — жилое помещение (М 1:10)

Применение: двери Д-2, Д-9, Д-13

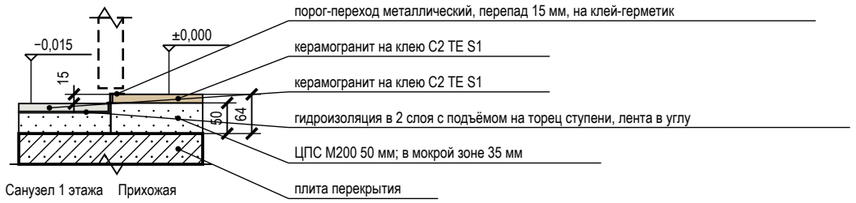


## 2 Стык покрытий пола Т-профилем без перепада (М 1:5)

Применение: проёмы 5↔11

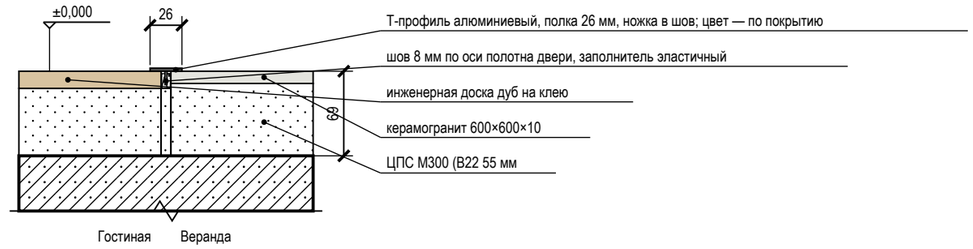


## 3 Дверь скрытого монтажа в плоскости стены, плинтус (М 1:5)

Применение: двери Д-1, Д-2, Д-7, Д-8, Д-9, Д-10, Д-11, Д-12, Д-13

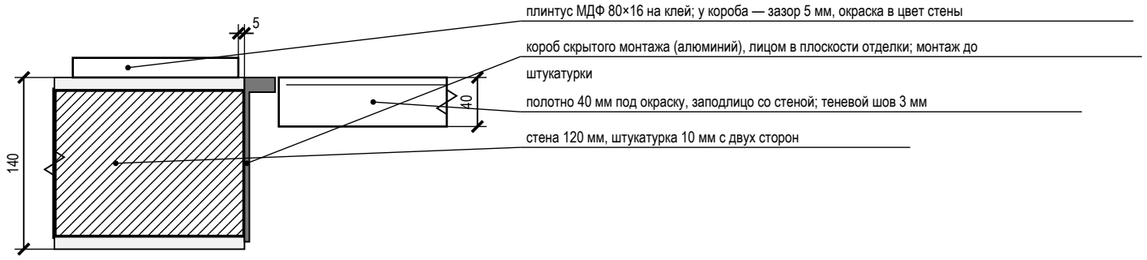


## 4 Короб стояков К1-1 с люком и звукоизоляцией (М 1:20)

Применение: пом. 3, 1, 8

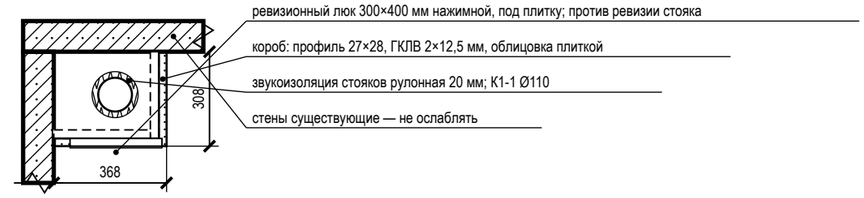


## 5 Гидроизоляция санузла: заход на стены 200 мм, примыкание ванны (М 1:20)

Применение: пом. 3, 15, 20

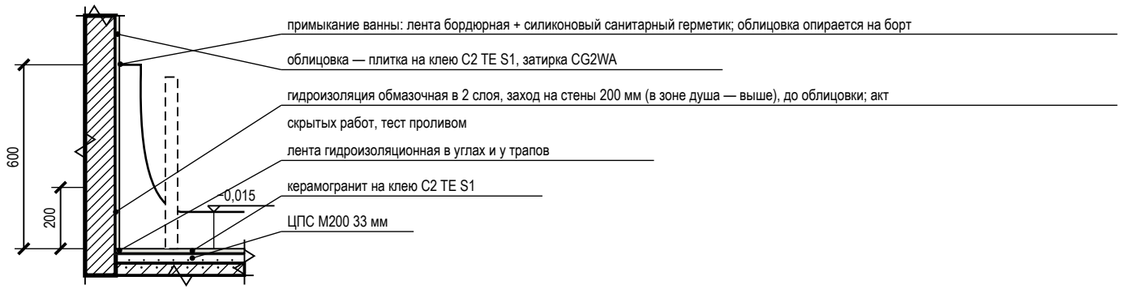


## 6 Плинтус МДФ 80×16 мм у окрашенной стены (М 1:10)

Применение: пом. 1, 2, 4, 5, 6, 7, 8, 9, 10, 13, 14, 16, 17, 18, 19

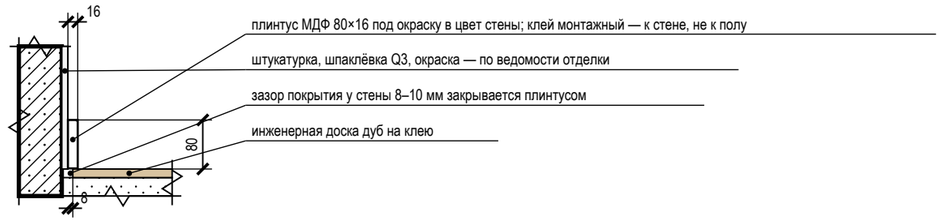


## Условные обозначения

- железобетон (плита, стены)
- кладка, перегородка
- стяжка, раствор
- гипсокартон ГКЛВ
- звукоизоляция, эластичный заполнитель
- плитка, керамогранит на клею
- инженерная доска (покрытие пола)
- металлический профиль (порог, Т-профиль, короб двери)
- гидроизоляция (обмазочная, лента)

## Примечания

1. Узлы — типовые решения проекта для мест, отмеченных выносками на листе схемы расположения развёрток и узлов; размеры — в мм, отметки — в м от ±0,000.
2. Узлы с гидроизоляцией, закладными и коробами скрытого монтажа принимаются по актам скрытых работ до закрытия отделкой; гидроизоляция — после теста проливом (24 ч).
3. Марки изделий (порог, Т-профиль, короб скрытой двери, люк) — по спецификациям; замена — на аналог с теми же габаритами по согласованию с автором проекта.

| | Лист | № док. | Подпись | Дата | Проект: Дом 331 м² | | | |
|---|---|---|---|---|---|---|---|---|
| Дизайнер | Кырлан А.С. | | | 19.10.26 | Узлы | Стадия | Лист | Листов |
| | | | | | | П | С3 | 156 |

выпуск 18.10.2026 № 8cd922c868 · стр. 156 из 156