ПРЕДВАРИТЕЛЬНО · не для производства работ · открыто пунктов: 9 (реестр — л. 6, 7)

L

LINEA

ДИЗАЙН-ПРОЕКТ ИНТЕРЬЕРА

Квартира 55 м²

кухня-гостиная и спальня



Визуализация кухни-гостиной · 3D

ОБЩАЯ ПЛОЩАДЬ	ПОМЕЩЕНИЙ	СТАДИЯ	ШИФР	ОСНОВА
55,23 м²	6, из них жилых 2	Рабочий проект · предварительно	ГД-2026-006-АИ	план заказчика, без обмера

ПАЛИТРА ОТДЕЛКИ

NCS S 1502-Y50	NCS S 1002-Y50	V503	G503	NCS S 2002-Y
44 %	32 %	24 %	текстиль, декор	текстиль, декор

АВТОР ПРОЕКТА

Кырлан Александр Сергеевич

Ноябрь 2026

Изм.	Кол.уч	Лист	№ док.	Подп.	Дата	ГД-2026-006-АИ		
						Квартира 58 м²		
						Общая площадь 55,23* м² · * размеры приняты, не замерены (реестр — л. 6, 7, К-5)		
Разраб.		Кырлан А.С.			14.11.26	Дизайн-проект интерьера	Стадия	Лист	Листов
Пров.							РП	1	108
ГИП									
Н. контр.						Титульный лист	Кырлан Александр Сергеевич		
Утв.						М б/м			

выпуск 14.11.2026 № bcee049e32 · стр. 1 из 128

Общие данные

Комплект ГД-2026-006-АИ · Квартира 58 м² · кухня-гостиная и спальня

ПРЕДВАРИТЕЛЬНО · не для производства работ · открыто пунктов: 9 (реестр — л. 6, 7)

Допущения и предложения на листе. См. лист открытых вопросов (листы 6, 7).

Ведомость рабочих чертежей основного комплекта ГД-2026-006-АИ

Лист	Наименование	Примечание
1	Титульный лист	
2	Общие данные	
3	Общие данные	
4	Общие данные	
5	Общие данные	
6	Открытые вопросы, принятые допущения и конфликты. Лист 1 из 2	
7	Открытые вопросы, принятые допущения и конфликты. Лист 2 из 2	
8	Задание на контрольный обмер и обследование. Лист 1 из 3	
9	Задание на контрольный обмер и обследование. Лист 2 из 3	
10	Задание на контрольный обмер и обследование. Лист 3 из 3	
11	График закупок и работ. Лист 1 из 3	
12	График закупок и работ. Лист 2 из 3	
13	График закупок и работ. Лист 3 из 3	
14	Календарный график работ и закупок	
15	Чек-лист приёмки по этапам. Лист 1 из 4	
16	Чек-лист приёмки по этапам. Лист 2 из 4	
17	Чек-лист приёмки по этапам. Лист 3 из 4	
18	Чек-лист приёмки по этапам. Лист 4 из 4	
19	Лист → мастер	
20	Обмерный план	
21	План демонтажа и монтажа перегородок	
22	План дверей и ведомость заполнения проёмов	
23	Концепция интерьера	
24	План расстановки мебели	
25	Спецификация мебели и оборудования	
26	Спецификация мебели и оборудования (продолжение)	
27	Спецификация мебели и оборудования (продолжение)	
28	План розеток и электровыводов	
29	План освещения	
30	План выключателей и схема включения	

Ведомость рабочих чертежей основного комплекта ГД-2026-006-АИ (продолжение)

Лист	Наименование	Примечание
31	Ведомость электроточек и изделий	
32	Однолинейная схема щита	
33	План принципиальных трасс	
34	Таблица нагрузок щита	
35	План слаботочных сетей	
36	План вентиляции	
37	План отопления	
38	План выводов сантехники	
39	Схема разводки водопровода и канализации	
40	Аксонометрическая схема В1 (холодное водоснабжение)	
41	Аксонометрическая схема Т3 (горячее водоснабжение)	
42	Аксонометрическая схема К1 (канализация)	
43	Развёртки мокрых зон: выводы ВК. Кухня-гостиная	
44	Развёртки мокрых зон: выводы ВК. Ванная	
45	Развёртки мокрых зон: выводы ВК. Санузел	
46	Спецификация сантехнического оборудования	
47	Техническое задание на подбор светильников	
48	План потолков	
49	Разрезы и узлы потолков	
50	Разрезы и узлы потолков (продолжение)	
51	Раскладка плитки. Планы полов	
52	Раскладка плитки. Прихожая	
53	Раскладка плитки. Ванная. Развёртки стен	

Общие указания — лист 5: ±0,000 — чистый пол; несущие конструкции и сети дома — по отдельному проекту; скрытые работы — по актам. Открытые вопросы и допущения — листы 6, 7.

Изм.	Кол.уч	Лист	№ док.	Подп.	Дата
Разраб.		Кырлан А.С.			14.11.26
Пров.					
ГИП					
Н. контр.					
Утв.					

ГД-2026-006-АИ

Квартира 58 м²

Общая площадь 55,23* м² · * размеры приняты, не замерены (реестр — л. 6, 7, К-5)

Дизайн-проект интерьера

Стадия	Лист	Листов
РП	2	108

Общие данные

М б/м

Кырлан Александр Сергеевич

выпуск 14.11.2026 № bcee049e32 · стр. 2 из 128

Общие данные

Комплект ГД-2026-006-АИ · лист 2 общих данных (продолжение)

ПРЕДВАРИТЕЛЬНО · не для производства работ · открыто пунктов: 9 (реестр — л. 6, 7)

Допущения и предложения на листе. См. лист открытых вопросов (листы 6, 7).

Ведомость рабочих чертежей основного комплекта ГД-2026-006-АИ (продолжение)

Лист	Наименование	Примечание
54	Раскладка плитки. Санузел. Развёртки стен	
55	План полов	
56	Ведомость отделки помещений	
57	Колерная карта	
58	Спецификация отделочных материалов	
59	Спецификация отделочных материалов	
60	Концепция декора и визуализации	
61	План текстиля и декора	
62	Шторы и карнизы	
63	Ведомость текстиля	
64	Ведомость декора. Схемы развески	
65	Схемы развески (продолжение)	
66	Встроенная мебель. Схема расположения	
67	Шкаф-купе М9	
68	Система хранения Г1	
69	Кухня (пом. 1). Развёртка гарнитура	
70	Кухня (пом. 1). Развёртка гарнитура: вид без фасадов и разрезы	
71	Кухня (пом. 1). Монтажная схема	
72	Кухня (пом. 1). Столешница: план	
73	Шкафы. Монтажная схема	
74	Ведомости изделий, техники и фурнитуры	
75	Сводка листовых материалов и кромки	
76	Реестр марок отделки и позиций альбома	
77	Схема расположения развёрток и узлов	
78	Развёртка стены В. Кухня-гостиная (пом. 1), кухонный фронт	
79	Развёртка стены А. Кухня-гостиная (пом. 1)	
80	Развёртка стены Б. Кухня-гостиная (пом. 1)	
81	Развёртка стены Г. Кухня-гостиная (пом. 1)	
82	Развёртка стены А. Спальня (пом. 2)	
83	Развёртка стены Б. Спальня (пом. 2)	

Ведомость рабочих чертежей основного комплекта ГД-2026-006-АИ (продолжение)

Лист	Наименование	Примечание
84	Развёртка стены В. Спальня (пом. 2)	
85	Развёртки стен А, Б. Ванная (пом. 3)	
86	Развёртки стен В, Г. Ванная (пом. 3)	
87	Развёртки стен А, Б. Санузел (пом. 4)	
88	Развёртки стен В, Г. Санузел (пом. 4)	
89	Развёртка стены А. Прихожая (пом. 5)	
90	Развёртки стен Б, Г. Прихожая (пом. 5)	
91	Развёртка стены В. Прихожая (пом. 5)	
92	Развёртка стены А. Гардеробная (пом. 6)	
93	Развёртки стен Б, Г. Гардеробная (пом. 6)	
94	Узлы	
95	Ведомость объёмов работ	
96	Ведомость объёмов работ (продолжение)	
97	Ведомость объёмов работ (окончание)	
98	Спецификация материалов	
99	Спецификация материалов (окончание)	
100	Смета ориентировочная	
101	Смета ориентировочная (окончание)	
102	Смета проекта: этапы, помещения, итог	
103	Смета проекта: этапы, помещения, итог (продолжение)	
104	Смета проекта: этапы, помещения, итог (окончание)	
105	Смета материалов с ценами	
106	Смета материалов с ценами (продолжение)	

Общие указания — лист 5: ±0,000 — чистый пол; несущие конструкции и сети дома — по отдельному проекту; скрытые работы — по актам. Открытые вопросы и допущения — листы 6, 7.

Изм.	Кол.уч	Лист	№ док.	Подп.	Дата
Разраб.		Кырлан А.С.			14.11.26
Пров.					
ГИП					
Н. контр.					
Утв.					

ГД-2026-006-АИ

Квартира 58 м²

Общая площадь 55,23* м² · * размеры приняты, не замерены (реестр — л. 6, 7, К-5)

Дизайн-проект интерьера

Стадия	Лист	Листов
РП	3	108

Общие данные

М б/м

Кырлан Александр Сергеевич

выпуск 14.11.2026 № bcee049e32 · стр. 3 из 128

Общие данные

Комплект ГД-2026-006-АИ · лист 3 общих данных (продолжение)

Ведомость рабочих чертежей основного комплекта ГД-2026-006-АИ (продолжение)

Лист	Наименование	Примечание
107	Смета материалов с ценами (продолжение)	
108	Смета материалов с ценами (окончание)	

Ведомость ссылочных и прилагаемых документов

Обозначение	Наименование	Примечание
	Ссылочные документы	
ГОСТ 21.201-2011	СПДС. Условные графические изображения элементов зданий, сооружений и конструкций	
ГОСТ 21.205-2016	СПДС. Условные обозначения элементов санитарно-технических систем	
ГОСТ 21.210-2014	СПДС. Изображения условные графические электрооборудования и проводок на планах	
ГОСТ 2.306-68	ЕСКД. Обозначения графические материалов и правила их нанесения на чертежах	
	Прилагаемые документы	
ГД-2026-006-АИ.В1	Визуализация. Интерьер: Ванная (пом. 3), стена Б	альбом визуализаций
ГД-2026-006-АИ.В2	Визуализация. Интерьер: Ванная (пом. 3), стена В	
ГД-2026-006-АИ.В3	Визуализация. Интерьер: Спальня (пом. 2), стена А	
ГД-2026-006-АИ.В4	Визуализация. Интерьер: Спальня (пом. 2), стена Б	
ГД-2026-006-АИ.В5	Визуализация. Интерьер: Прихожая (пом. 5), общий вид	
ГД-2026-006-АИ.В6	Визуализация. Интерьер: Кухня-гостиная (пом. 1), стена Б	
ГД-2026-006-АИ.В7	Визуализация. Интерьер: Кухня-гостиная (пом. 1), стена В	
ГД-2026-006-АИ.В8	Визуализация. Интерьер: Кухня-гостиная (пом. 1), стена Г	
ГД-2026-006-АИ.В9	Визуализация. Интерьер: Гардеробная (пом. 6), общий вид	
ГД-2026-006-АИ.В10	Визуализация. Интерьер: Санузел (пом. 4), общий вид	

Состав дизайн-проекта

Раздел	Состав	Листы
Обложка	Дизайн-проект интерьера; Квартира 58 м²; автор проекта — Кырлан Александр Сергеевич	1 с.
Концепция	Стиль Скандинавский: концепция интерьера, палитра и материалы (колерная карта лист 57)	л. 23
Визуализации	10 изобр.: Ванная, стена Б; Ванная, стена В; Спальня, стена А; Спальня, стена Б; Прихожая, общий вид; Кухня-гостиная, стена Б; Кухня-гостиная, стена В; Кухня-гостиная, стена Г; Гардеробная, общий вид; Санузел, общий вид	В1–В10
Рабочие чертежи	планы, развёртки, узлы (развёртки и узлы — листы 43–45, 77, 85–88, 90, 93, 94)	л. 1–108
Спецификации и ведомости	оборудование, изделия, отделка, электроточки	л. 22, 25–27, 31, 46, 56–59, 63, 64, 95–99

Допущения и предложения на листе

Основа листа: размеры сняты с плана заказчика, контрольный обмер не выполнен (К-5); высота потолка 2700 мм принята: на плане заказчика не указана (К-5); подрайон климата не задан — принят не северный (жилые от 2,5 м) (К-4); толщины стен приняты: наружные 250 мм, перегородки 120 мм — не обмерены (К-5); разрешённая мощность 15 кВт принята по типовой квартире, технических условий нет (К-6).

См. лист открытых вопросов (лист 6, записи К-4–К-6).

Общие указания — лист 5: ±0,000 — чистый пол; несущие конструкции и сети дома — по отдельному проекту; скрытые работы — по актам. Открытые вопросы и допущения — листы 6, 7.

Изм.	Кол.уч	Лист	№ док.	Подп.	Дата
Разраб.		Кырлан А.С.			14.11.26
Пров.					
ГИП					
Н. контр.					
Утв.					

ГД-2026-006-АИ

Квартира 58 м²

Общая площадь 55,23* м² · * размеры приняты, не замерены (реестр — л. 6, 7, К-5)

Дизайн-проект интерьера

Стадия	Лист	Листов
РП	4	108

Общие данные

М б/м


Кырлан Александр Сергеевич

выпуск 14.11.2026 № bcee049e32 · стр. 4 из 128

Общие данные

Комплект ГД-2026-006-АИ · лист 4 общих данных (продолжение)

Условные обозначения

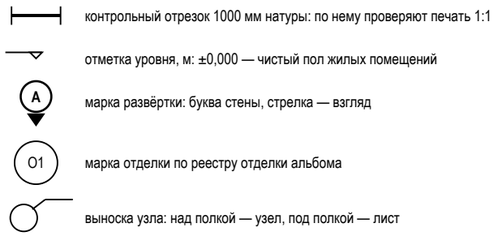

контрольный отрезок 1000 мм натуры: по нему проверяют печать 1:1

отметка уровня, м: ±0,000 — чистый пол жилых помещений

марка развёртки: буква стены, стрелка — взгляд

марка отделки по реестру отделки альбома

выноска узла: над полкой — узел, под полкой — лист

Общие указания

1. Рабочие чертежи интерьера разработаны на основании задания на проектирование и обмерного плана (лист 20). Объект: Квартира 58 м²; автор проекта — Кырлан Александр Сергеевич; общая площадь 55,23 м², жилая 34,99 м², помещений 6.
2. Рабочие чертежи выполнены в соответствии с заданием на проектирование и нормативными документами, перечисленными в п. 4.
3. Открытые вопросы, принятые допущения и конфликты между разделами, не снятые к выпуску комплекта, сведены в таблицы на листах 6, 7. До ответа по пункту таблицы показанное на указанном там листе — допущение, а не утверждённое решение: комплект по этим листам предварительный.
4. Нормативные документы, на которые есть ссылки в листах комплекта: ГОСТ Р 21.101-2026; ГОСТ 21.501-2018; ГОСТ 2.302-68; ГОСТ 2.303-68; ГОСТ 2.304-81; ГОСТ 2.307-2011; СП 54.13330.2022; СП 71.13330.2017; СП 73.13330.2016; ПУЭ (7-е изд.), гл. 1.8, 7.1; ГОСТ Р 50571.7.701-2024; СанПиН 1.2.3685-21; ГОСТ 2.702; ГОСТ 2.755; ГОСТ 21.110-2013; ГОСТ 21.601; ГОСТ 13996-2019; ГОСТ 23166-2021; ГОСТ 31173-2016; ГОСТ 31565-2012; ГОСТ 32414-2013; ГОСТ 32415-2013; ГОСТ Р 56387-2018; СП 29.13330.2011; СП 30.13330.2020; СП 51.13330.2011; СП 131.13330; СП 163.1325800.2014; СП 256.1325800.2016. Документы из ведомости ссылочных документов здесь не повторяются.
5. За отметку ±0,000 принят уровень чистого пола жилых помещений квартиры (относительная отметка; абсолютная — по проекту дома). Отметка чистого пола мокрых помещений — −0,015. Размеры — в миллиметрах, отметки — в метрах, площади — в м²; высоты установки Н от чистого пола своего помещения до оси изделия.
6. Несущие конструкции, общедомовые стояки, вентиляционные каналы и инженерные сети дома настоящим комплектом не изменяются. Работы, затрагивающие их (проём или штраба в несущей стене, перенос стояка, врезка в вентканал, расширение мокрой зоны), выполняются только по отдельному проекту, к которому прилагается техническое заключение о допустимости и безопасности работ, выданное автором проекта дома или организацией с допуском на обследование, и который согласован в установленном порядке (Жилищный кодекс РФ, ст. 25–29).
7. Трассы инженерных сетей на листах — принципиальные. Расчёты электрических нагрузок и токов КЗ, гидравлики, воздухообмена, освещённости и нагрузок на перекрытие выполняются в проектах ЭОМ, ВК, ОВ и КР организацией с допуском СРО; фактические трассы до закрытия отделкой фиксируются исполнительными схемами.
8. Стиль интерьера — Скандинавский. Палитра проекта: основной — NCS S 1502-Y50R «S 1502-Y50R», NCS S 1002-Y50R «S 1002-Y50R», NCS S 0300-N «S 0300-N»; дополнительный — Tikkurila V503 «Winter»; акцент — NCS S 4010-R90B «S 4010-R90B». Коды цвета — по веерам производителей; цвет утверждается по выкрасу на объекте при освещении проекта.
9. Площади поверхностей — по чистым граням стен до отделки: стены = периметр × высоту от чистого пола помещения до низа потолка минус проёмы (облицовка плиткой — до верха облицовки); плинтус = периметр минус дверные проёмы; пол и потолок — по площади помещения. Количество плиток — по раскладке. Способ один для всех листов комплекта (ведомость отделки, колерная карта, раскладка плитки, развёртки).
10. Марки: стены помещения на всех листах — А (верхняя по плану), Б (правая), В (нижняя), Г (левая); марка отделки О — одна на весь альбом; реестр марок отделки (с позициями колерной карты той же отделки) и марки позиций по видам — на листе 76.
11. Развёртки стен выполнены по всем помещениям для стен с электроточками, мебелью, декором и отделкой: санузлы и кухонный фронт — в М 1:25, остальные стены — в М 1:25; расположение развёрток и узлов — на листе 77, узлы — на листе 94.
12. Перечень скрытых работ, на которые составляются акты освидетельствования (форма по приказу Минстроя России № 344/пр): гидроизоляция пола и стен мокрых помещений (с тестом проливом); стяжка пола (толщина, прочность, влажность основания); тёплый пол до заливки (сопротивление, схема укладки); скрытая электропроводка (за потолком и в штробах стен; условия штробления — в следующем пункте); трубопроводы водоснабжения и канализации до закрытия (опрессовка, уклоны); закладные и усиления под подвесные приборы, мебель и тяжёлый декор, рамы инсталляций; короба дверей скрытого монтажа до штукатурки; каркасы ГКЛ потолков, коробов и перегородок до обшивки.
13. Скрытая электропроводка: за потолком и в штробах стен. Штробы в стенах выполняются только после технического заключения о несущих конструкциях; до заключения несущие стены не определены, и все стены считаются несущими; объём штроб — в ведомости объёмов работ, строка «Штробы в стенах» (вертикальные спуски; объём не меньше фактического, горизонтальные трассы — по исполнительной схеме).
14. Критерии приёмки: допуски отделочных покрытий — по СП 71.13330.2017; испытания систем водоснабжения и канализации — по СП 73.13330.2016 до закрытия трасс; приёмо-сдаточные испытания электроустановки — по ПУЭ, гл. 1.8, с протоколом электролаборатории.
15. Осознанные отступления от ГОСТ Р 21.101-2026, принятые в комплекте: номер листа и число листов («Листов») указаны на каждом листе; на масштабных листах в основной надписи указан фактический масштаб и дан контрольный отрезок 1000 мм; развёртки стен выполнены в М 1:25 (ГОСТ 21.507-81 — 1:50…1:500) ради читаемости привязок; размерные числа и марки элементов (Д-1, ОК-1, О6) кеглем 2,5 мм, номера помещений — в кружке Ø 8 мм (канон — 3,5 мм и Ø 12 мм): так насыщенные листы А3 читаются без наложений надписей.
16. Графы «Пров.», «Н. контр.», «Утв.» основной надписи заполняются при согласовании комплекта с заказчиком; до согласования комплект подписывает автор проекта (графа «Разраб.»).

Допущения и предложения на листе

Основа листа: размеры сняты с плана заказчика, контрольный обмер не выполнен (К-5); высота потолка 2700 мм принята: на плане заказчика не указана (К-5); подрайон климата не задан — принят не северный (жилые от 2,5 м) (К-4); толщины стен приняты: наружные 250 мм, перегородки 120 мм — не обмерены (К-5); разрешённая мощность 15 кВт принята по типовой квартире, технических условий нет (К-6).

См. лист открытых вопросов (лист 6, записи К-4–К-6).

						ГД-2026-006-АИ	
						Квартира 58 м²	
						Общая площадь 55,23* м² · * размеры приняты, не замерены (реестр — л. 6, 7, К-5)	
Изм.	Кол.уч	Лист	№ док.	Подп.	Дата		
Разраб.		Кырлан А.С.			14.11.26	Дизайн-проект интерьера	Стадия: РП; Лист: 5; Листов: 108
Пров.							
ГИП							
						Общие данные М б/м	**Кырлан Александр Сергеевич**
Н. контр.							
Утв.							

выпуск 14.11.2026 № bcee049e32 · стр. 5 из 128

Открытые вопросы, принятые допущения и конфликты. Лист 1 из 2

Сводка по реестрам координации

ПРЕДВАРИТЕЛЬНО · не для производства работ · открыто пунктов: 9 (реестр — л. 6, 7)

Комплект предварительный по пунктам этих таблиц. Пока по пункту нет ответа или решения, показанное на указанном листе — допущение проектировщика, а не утверждённое решение.
Сводка: открытых вопросов — 7 (из них ждут факта объекта — 6: контрольного обмера, обследования или документа); изменений в реестре — 5, из них без подписи — 2.
Пункты, ответ на которые лежит на объекте, а не за столом проектировщика (графа «Вид», строка «Ждёт»), собраны на листе «Задание на контрольный обмер и обследование» (листы 8–10): что и где замерить, с какой точностью и чем подтвердить. Пункты, ждущие решения человека, на объекте не закрываются.

Открытые вопросы и принятые допущения

№	Формулировка	Вид	Кто решает	Если решения нет	Лист, где это проявляется
К-1	Вентканалы на плане заказчика не показаны: ВК-1 принят у перегородки ванной и санузла (со стороны прихожей), ВК-2 — у кухни. От них зависят решётки ВР1–ВР3 и короба. Замерить положение и сечение каналов, проверить тягу.	Отсутствует Ждёт: обмера	Инженер ОВ	решётки ванной и санузла — у ВК-1, кухни — у ВК-2; места — до обмера, лист перевыпустить по факту	л. 36 — План вентиляции
К-2	Ванная (пом. 3), 2140 × 1380 мм в чистоте, проём Д-4 у стены Б. Расстановка проектировщика: ванна 1500 × 700 у стены А от стены Г (была 1600 и заходила в проход перед Д-4 — свободно 240 из 700 мм), умывальник П3 у стены В справа от ванны — перед ним свободно 750 мм (был напротив ванны в 230 мм), полотенцесушитель П5 на стене В между коробом стояков и умывальником. Унитаз П2 из образца раскладки снят: он стоял на стояке Ст К1-1 (короба и люка не поставить), унитаз квартиры — П20 в санузле, инсталляция и короб — там. Остаётся: перед ванной 680 мм до стены В при ориентире 750 мм — это глубина помещения; у умывальника до стены Б 90 мм при ориентире 200 мм. Решить: (а) принять расстановку; (б) душ с поддоном 900 × 900 у стены Г вместо ванны — перед приборами ≥ 750 мм, кадры ванной перерисовать; (в) другой вариант автора.	Спорно Ждёт: решения	Инженер ВК (вода, канализация)	ванна 1500 × 700 и умывальник у стены В по листам; модели ванны и умывальника не заказывать до решения	л. 38 — План выводов сантехники л. 24 — План расстановки мебели
К-3	Скрытые двери Д-2, Д-3, Д-4 стоят в существующих проёмах прихожей, размеров в свету нет: короб скрытой двери шире и выше полотна на 100–120 / 50–80 мм, полотно по проёму 2100 под ряд 2000 не встаёт (по каталогам нужно 2050–2080). У Д-3 (спальня) и Д-4 (санузел) откос от угла 40 мм — под короб нужно не меньше 50. Замерить проёмы в чистоте и откосы; решить: проёмы подрезать/расширить на 10+ мм от угла (если стена не несущая) или взять модель с узким коробом; высоту проёма — по выбранной модели.	Отсутствует Ждёт: обмера, затем решения	Архитектор-планировщик	блоки скрытых дверей не заказывать до замера; полотна на листах — расчётные («расч.»), проёмы не переносятся	л. 22 — План дверей и ведомость заполнения проёмов
К-4	Климатический подрайон (СП 131.13330) не задан: принят не северный — жилые комнаты и кухня под потолком от 2,5 м (СП 54, п. 5.12); в IA, IБ, IГ, IД, IVA — от 2,7 м.	Отсутствует Ждёт: документа	Архитектор-планировщик	отметки потолков жилых — по 2,5 м; при северном подрайоне уровни ниже 2,7 м пересчитать до заказа каркаса	л. 48 — План потолков
К-5	Основа альбома — план заказчика без контрольного обмера: размеры помещений сняты с плана, высота потолка 2700 мм и толщины стен (наружные 250 мм, перегородки 120 мм) приняты — на плане они не указаны. От них зависят вертикальные размеры (развёртки, шкафы, плитка, потолки), объёмы работ и сборка шкафов-купе. Выполнить контрольный обмер.	Непонятно Ждёт: обмера	Архитектор-планировщик	размеры, высота потолка и толщины стен — принятые; мебель на заказ, двери и каркас потолков не заказывать до обмера	л. 20 — Обмерный план
К-6	Разрешённая мощность 15 кВт принята по типовой квартире, технических условий в материалах объекта нет. Сверить с техническими условиями.	Непонятно Ждёт: документа	Инженер-электрик	вводной аппарат и группы щита — по 15 кВт; при меньшей мощности схему щита пересчитать до монтажа	л. 32 — Однолинейная схема щита
К-7	Места стиральной машины в квартире не было. В ванной 2,2 × 1,5 м и санузле места 600 × 600 с подходом нет. Предложение исполнителя: узкая машина 600 × 450 под столешницей кухни вместо модуля с ящиками М11 справа от варочной, ряд удлиняется на 220 мм; отдельная группа щита с УЗО 30 мА. Решить: принять, или машина в ванной вместо ванны (душ), или отказ от машины (прачечная) решением автора	Предложение Ждёт: документа, затем решения	Инженер ВК (вода, канализация)	стиральная машина П6 в кухне под столешницей (ниша вместо М11, 2800…3420) — как на листах	л. 38 — План выводов сантехники л. 24 — План расстановки мебели л. 32 — Однолинейная схема щита

Изм.	Кол.уч	Лист	№ док.	Подп.	Дата
Разраб.		Кырлан А.С.			14.11.26
Пров.					
ГИП					
Н. контр.					
Утв.					

ГД-2026-006-АИ

Квартира 58 м²

Общая площадь 55,23* м² · * размеры приняты, не замерены (реестр — л. 6, 7, К-5)

Дизайн-проект интерьера

Стадия	Лист	Листов
РП	6	108

Открытые вопросы, принятые допущения и конфликты. Лист 1 из 2
М б/м

Кырлан Александр Сергеевич

выпуск 14.11.2026 № bcee049e32 · стр. 6 из 128

Открытые вопросы, принятые допущения и конфликты. Лист 2 из 2

Сводка по реестрам координации

Изменения проекта после выпуска листов (реестр изменений)

№	Дата	Лист	Было	Стало	Кто решил, подпись
ИЗ-1	30.10.2026	л. 28 — План розеток и электровыводов л. 30 — План выключателей и схема включения л. 29 — План освещения л. 74 — Ведомости изделий, техники и фурнитуры	Кухня-гостиная: ТВ1, LAN1 и розетка «ТВ, приставка» стояли на стене В (привязка 3300…3450, кухонная стена), а ТВ-тумба М20 — на стене Г (1500…3300): за телевизором точек не было. Выключатель S1 — на стене Г в зоне экрана, у двери Д-2 выключателя не было. Светильник гардеробной Св16 — на линии L6 подсветки кухонной столешницы, выключателя в гардеробной нет. Ванная и санузел — одна линия L4 с одним выключателем S4. Вытяжка в М10 без вывода питания; розетка холодильника без привязки к модулю М4.	ТВ1 (2400), LAN1 (2550) и розетка приставки (2400, H=300) — на стене Г по оси тумбы М20. S1 стена В, привязка 4950 (150 мм от проёма Д-2 со стороны ручки), S5 у дивана — проходной. Св16 — линия L7, выключатель S8 на стене Г гардеробной у Д-3 (привязка 1500). Санузел — линия L9, выключатель S9 в прихожей у Д-4 санузла (стена Г, привязка 1450); S4 — только ванная (L4, вентилятор ВР2). Розетка вытяжки — стена В привязка 2500, H=2200, группа 2 (для М10); розетка холодильника — для М4.	Утверждено: Кырлан А.С., 12.11.2026. Предложил: исполнитель.
ИЗ-2	30.10.2026	л. 24 — План расстановки мебели л. 25 — Спецификация мебели и оборудования	Диван М1 на стене Б привязка 1300…3500: торец в 500 мм от стены В, дверь Д-2 (3900…4800) открывалась в торец дивана. Кресло М22 х 4250, у 450.	Диван М1 привязка 1000…3200 — перед проёмом 800 мм; кресло М22 х 3500…4300, у 450 у окна 2. Выключатель S5 и розетка у дивана — привязка 900. Знак «**» у М1, М22 до подписи автора.	Утверждено: Кырлан А.С., 12.11.2026. Предложил: исполнитель.
ИЗ-3	30.10.2026	л. 36 — План вентиляции	Внутренний блок КВ-1 на стене А привязка 3300…4200 — внутри оконного проёма 3200…4800; наружный КН-1 привязка 3350 — на окне.	КВ-1 — стена Г, привязка 300…1200 (простенок у окна 1), КН-1 — стена А, простенок между окнами 2400…3200. Трасса ≈ 3 м (петля принята по минимуму, паспорта модели нет). Знак «**» у КВ-1 до подписи автора.	Утверждено: Кырлан А.С., 12.11.2026. Предложил: исполнитель.
ИЗ-4	12.11.2026	л. 61 — План текстиля и декора л. 63 — Ведомость текстиля л. 64 — Ведомость декора. Схемы развески л. 62 — Шторы и карнизы	Декор и текстиль в данных проекта не были заданы: ни штор, ни ковров, ни подушек и пледов, ни картин, зеркал и растений (в палитре — пометка «текстиль в данных ещё не задан»). Кадры визуализаций и листы декоратора строятся только по данным — помещения выходили пустыми; зеркал в прихожей и над умывальником ванной не было.	Декор и текстиль заданы позициями плана. Кухня-гостиная: шторы льняные в пол на оба окна (Т1, Т2; шина на потолке, вынос 250 — зазор до радиаторов 110 мм), ковёр шерстяной 1400×2500 в зоне дивана (Т3), подушки 3 + 2 и плед на диван М1 (Т4–Т6), пара постеров в дубовых рамах 600×800 над диваном (ДК1, ДК2; низ 1050), фикус в напольном кашпо в углу у окна 1 (ДК3), ваза на обеденном столе М3 (ДК4). Спальня: римская штора с блэкаутом (Т7; в пол не идёт — слева внутренний блок КВ-2, под окном радиатор), ковёр 2000×3000 под кроватью (Т8), подушки 2 + 1 и плед на кровать С1 (Т9–Т11), картина 1100×700 над изголовьем, зеркало в рост 600×1600 на стене В (ДК6), замиокулькас в углу (ДК7). Ванная: зеркало 450×650 над умывальником П3 (ДК8). Санузел: постер 300×400 на стене В (ДК9). Прихожая: зеркало в рост 600×1700 на стене А слева от двери Д-2 (ДК10), постер 400×560 в простенке между дверями Д-2 и Д-3 (ДК11). Цвета — из палитры стиля: молочный, каменный, акценты — пыльный синий NCS S 4010-R90B и шалфей NCS S 3010-G10Y. Дорожка в прихожей не задана: весь пол — в зонах открывания пяти дверей. Знак «**» у позиций до подписи автора.	Не утверждено: подписи нет. решение исполнителя; предложение проектировщика, на утверждение А. С. Кырлана
ИЗ-5	12.11.2026	л. 61 — План текстиля и декора л. 63 — Ведомость текстиля л. 64 — Ведомость декора. Схемы развески	Разбор двух критиков по кадрам: мокрые зоны — «стерильный шоурум»: в ванной на полотенцесушителе П5 нет полотенец, у ванны нет коврика, в санузле на полке короба инсталляции пусто (ИЗ-4 задал там только зеркало и постер).	Ванная: банные полотенца пыльного синего и ручные молочные на полотенцесушителе П5 (Т12, Т13), коврик 800×450 у бортика ванны (Т14; вне полотна двери Д-4). Санузел: ваза с сухой веткой и свеча с диффузором на полке короба инсталляции П20 (ДК12, ДК13). Смеситель ванны П1 в данных задан («смеситель настенный») — правка не нужна. Прихожая не дополнялась: стены заняты дверями, щитами и домофоном, пол — в зонах открывания пяти дверей (см. ИЗ-4). Знак «**» у позиций до подписи автора.	Не утверждено: подписи нет. решение исполнителя; предложение проектировщика, на утверждение А. С. Кырлана

Примечания

1. Номера листов — по ведомости рабочих чертежей комплекта (лист «Общие данные»).
2. Графа «Если решения нет» показывает состояние решения на листах; влияние на сроки и стоимость по пунктам не оценивалось.
3. Пункт, по которому принято решение, при следующем выпуске комплекта из таблиц исключается.

Изм.	Кол.уч	Лист	№ док.	Подп.	Дата
Разраб.		Кырлан А.С.			14.11.26
Пров.					
ГИП					
Н. контр.					
Утв.					

ГД-2026-006-АИ

Квартира 58 м²

Общая площадь 55,23* м² · * размеры приняты, не замерены (реестр — л. 6, 7, К-5)

Дизайн-проект интерьера

Стадия	Лист	Листов
РП	7	108

Открытые вопросы, принятые допущения и конфликты. Лист 2 из 2

М б/м

Кырлан Александр Сергеевич

выпуск 14.11.2026 № bcee049e32 · стр. 7 из 128

Задание на контрольный обмер и обследование. Лист 1 из 3

ПРЕДВАРИТЕЛЬНО · не для производства работ · открыто пунктов: 9 (реестр — л. 6, 7)

Что замерить, вскрыть и получить до заказа материалов и изделий

Задание собрано из открытых вопросов, ответ на которые лежит на объекте или в документах, а не за столом проектировщика. Пока факт не получен, размер, материал или положение на листах — допущение (знак «*»), а не замер.
Сводка: на объекте — 9 (до демонтажа — 7; после демонтажа — 2); документом и при закупке — 4; из допущений в данных и на листах — 9, из них без вопроса в реестре — 6. Закрываются вопросы: К-1, К-3–К-7 (6). Вопросы, ждущие решения человека, задание не закрывает — они решаются по реестру открытых вопросов.

Условия проведения

Порядок работ	Приёмы и точность	Кто присутствует	Если факт не совпал с проектом
1. До демонтажа — существующее состояние: контур, диагонали, высоты, проёмы, оси стояков, ниши и конструкции, которые видны. 2. После демонтажа, до черновых работ — то, что закрывали отделка и короба: основание стен, фактические толщины, углы, узлы. 3. Документы и данные закупки — не на объекте: к сроку из последней таблицы, от них зависят привязки и заказ. Что заказывается по размеру из задания, до закрытия пункта не заказывают: сроки изготовления — по графику закупок прораба.	Обход по часовой стрелке от входа: стены, проёмы, потолок, коммуникации (стояки, щиток, вентканалы), особенности (ниши, короба, выступы). Размеры записывают в мм; сумма участков равна общему размеру, при цепочке длиннее трёх участков ставят проверочный (общий) размер. Диагонали каждого помещения; если две диагонали различаются на 5 мм и больше, разницу подписывают на плане. Потолок — в нескольких точках: центр, углы, у проёмов. Проём — ширина, высота, глубина откоса, привязка к ближайшим углам, высота подоконника. Допустимая погрешность прибора — 2–3 мм на метр; размеры округляют кратно 5 мм; два контрольных промера одного размера не должны расходиться более чем на 2 %. Допуск по пункту — в графе «Точность». План БТИ обмер не заменяет.	Прораб (отвечает за проведение) — назначает день и порядок обхода, открывает объект и освобождает помещения, ведёт это задание и реестр изменений. Архитектор — выполняет обмер, составляет акт контрольного обмера и подписывает результаты по размерам и конструкциям. Владельцы вопросов присутствуют при пунктах своего раздела или принимают результат до заказа: Инженер ОВ — К-1; позиции О-13, О-3; Инженер-электрик — К-6; позиции О-2; Инженер ВК (вода, канализация) К-7; позиции О-1; Отделочник — позиции О-8, О-9. Заказчик или его представитель — передаёт документы (план БТИ, проект дома, технические условия, паспорта), подписывает акт. Проектных решений на обмере не принимают: обмер даёт факт, решения — по реестру открытых вопросов (листы 6–7).	1. В пределах допуска пункта — принимается измеренное значение, лист перевыпускается, знак «*» снимается. 2. Больше допуска или контрольные промеры расходятся более чем на 2 % — промер повторяют; не подтвердилось — запись в реестр изменений (дата, лист, было, стало, кто решил, подпись), работы в этом месте не начинают. 3. Затронуты несущая стена, стояк, вентканал или мокрая зона — сразу владельцу раздела и ГИПу (главному инженеру проекта); между разделами не больше двух кругов, затем решает ГИП. 4. На объекте устно ничего не согласуется: каждое решение — записью в реестр с подписью.

Этап 1. До демонтажа

№	Где	Способ	Что сделать	Кто выполняет	Точность	Что пересчитается в альбоме	Чем подтверждается	Закрывает вопросы реестра
О-1	Ввод В1 и Т3** у стояков; по всей квартире	Обмер	Отключающая арматура и счётчики воды на вводах: положение, тип, пломбы управляющей компании. Альбом ставит их на каждом вводе по практике, в данных их нет.	Архитектор	±5 мм	Узлы ввода в спецификации ВК (краны, фильтры, счётчики); места ввода на плане выводов. Листы: л. 38 — План выводов сантехники л. 46 — Спецификация сантехнического оборудования	акт контрольного обмера; фото с рулеткой и привязкой к стене или углу	Вопроса в реестре нет: Альбом принимает счётчики воды на вводах без осмотра. Результат принимает: Инженер ВК (вода, канализация)
О-2	Вход в квартиру или лестничная клетка; место щита на плане	Обмер	Существующий щиток и счётчик электроэнергии: место и габарит ниши, состояние ввода, марка и сечение вводного кабеля, наличие вводного автомата и УЗО, пломбы.	Архитектор	±5 мм	Ниша и место щита на листах; вводной кабель и аппараты на однолинейной схеме; расстояния до первых групп. Листы: л. 32 — Однолинейная схема щита	акт контрольного обмера; фото с рулеткой и привязкой к стене или углу	Вопроса в реестре нет: Альбом принимает щит и ввод без осмотра. Результат принимает: Инженер-электрик
О-3	у окон	Обмер	Положение стояков отопления (подающий и обратный) от граней стен, диаметры, наличие запорной арматуры; существующие радиаторы: число секций, межосевое расстояние, подводки. В данных стояков отопления нет — лист отопления выводит их условно у откоса окна.	Архитектор	±5 мм	План отопления: места стояков и подводок, привязки радиаторов; подбор радиаторов по теплотехническому расчёту; радиаторы и узлы подключения в ВОР и спецификации. Листы: л. 37 — План отопления	акт контрольного обмера; фото с рулеткой и привязкой к стене или углу	Вопроса в реестре нет: Альбом принимает положение стояков и радиаторов отопления без обмера. Результат принимает: Инженер ОВ

Допущения и предложения на листе
Основа листа: размеры сняты с плана заказчика, контрольный обмер не выполнен (К-5); высота потолка 2700 мм принята: на плане заказчика не указана (К-5); подрайон климата не задан — принят не северный (жилые от 2,5 м) (К-4); толщины стен приняты: наружные 250 мм, перегородки 120 мм — не обмерены (К-5); разрешённая мощность 15 кВт принята по типовой квартире, технических условий нет (К-6).
Знак «**» — предложение проектировщика, заказчиком не утверждено (согласовать с заказчиком): ИЗ-4: Т3.
См. лист открытых вопросов (лист 6, записи К-4–К-6; лист 7, запись ИЗ-4).

Изм.	Кол.уч	Лист	№ док.	Подп.	Дата
Разраб.		Кырлан А.С.			14.11.26
Пров.					
ГИП					
Н. контр.					
Утв.					

ГД-2026-006-АИ

Квартира 58 м²

Общая площадь 55,23* м² · * размеры приняты, не замерены (реестр — л. 6, 7, К-5)

Дизайн-проект интерьера

Стадия	Лист	Листов
РП	8	108

Задание на контрольный обмер и обследование.
Лист 1 из 3
М б/м

Кырлан Александр Сергеевич

выпуск 14.11.2026 № bcee049e32 · стр. 8 из 128

Задание на контрольный обмер и обследование. Лист 2 из 3

Что замерить, вскрыть и получить до заказа материалов и изделий

Этап 1. До демонтажа (продолжение)

№	Где	Способ	Что сделать	Кто выполняет	Точность	Что пересчитается в альбоме	Чем подтверждается	Закрывает вопросы реестра
О-4	санузел, ванная, кухня	Обмер	Положение и сечение вентканалов (вентблока), тяга.	исполнитель	±10 мм	план вентиляции, потолки, короба Листы: л. 36 — План вентиляции	акт контрольного обмера	К-1 Результат принимает: Инженер ОВ
О-5	прихожая (пом. 5)	Обмер	Проёмы Д-2, Д-3, Д-4 в чистоте (ширина, высота от чистого пола) и откосы до углов прихожей.	исполнитель	±5 мм	ведомость заполнения проёмов, план дверей Листы: л. 22 — План дверей и ведомость заполнения проёмов	акт контрольного обмера	К-3 Результат принимает: Архитектор
О-6	По месту	Обмер	Подтвердить на объекте принятое: подрайон климата не задан — принят не северный (жилые от 2,5 м)	Архитектор	±5 мм	Листы, где используется принятая величина. Листы: л. 2–5 — Общие данные	акт контрольного обмера	К-4 Результат принимает: Архитектор
О-7	все помещения квартиры	Обмер	Контрольный обмер всех помещений: стороны, диагонали, проёмы, толщины стен; высота потолка в каждом помещении в нескольких точках (центр, углы, у проёмов). Принято: потолок 2700 мм, стены 250 / 120 мм.	исполнитель	±5 мм	обмерный и монтажный планы, развёртки, план потолков, шкафы, объёмы работ Листы: л. 20 — Обмерный план	акт контрольного обмера	К-5 Результат принимает: Архитектор

Этап 2. После демонтажа, до черновых работ

№	Где	Способ	Что сделать	Кто выполняет	Точность	Что пересчитается в альбоме	Чем подтверждается	Закрывает вопросы реестра
О-8	Кухня-гостиная (пом. 1), Спальня (пом. 2), Ванная (пом. 3), Санузел (пом. 4), Прихожая (пом. 5), Гардеробная (пом. 6)	Обмер	Нивелировка плиты перекрытия и существующего пола после демонтажа покрытий: отметки в углах и по сетке, перепады по помещению, уклоны, отметки порогов (чистый пол в мокрых зонах принят -15 мм, 0 мм). Принятая толщина стяжки 33 мм, 50 мм и отметка чистого пола — расчётные, не от замера плиты.	Архитектор	±5 мм по отметке; ровность просвет под 2-метровой рейкой, горизонталь против 0,2 % длины помещения	Толщина стяжки и отметка чистого пола; уклоны к трапам и пороги; выпуски К1 относительно чистого пола (план разводки); объёмы стяжки и смеси в ВОР и спецификации. Листы: л. 51, 55 — План полов л. 39 — Схема разводки водопровода и канализации	акт контрольного обмера	Вопроса в реестре нет: Альбом принимает отметки плиты и толщину пирога пола без нивелировки. Результат принимает: Отделочник
О-9	Кухня-гостиная (пом. 1), Спальня (пом. 2), Ванная (пом. 3), Санузел (пом. 4), Прихожая (пом. 5), Гардеробная (пом. 6)	Обмер	Вертикаль и плоскостность стен: отклонение от вертикали по высоте стены (отвес или лазерный уровень), просвет под правилом 2 м, кривизна углов. Нужно там, где от стены зависит изделие: облицовка плиткой (пом. 3, 4), штукатурка и окраска (пом. 1, 2, 5, 6), встроенная мебель и кухня (пом. 1, 5).	Архитектор	до 1 мм на 2 м (правило и клиновой щуп); вертикаль — мм на высоту стены, отклонения подписываются на плане	Толщина штукатурки и расход смеси в ВОР и спецификации; раскладка плитки (подрезка у стен); зазоры и крепление встроенной мебели и кухни. Листы: л. 51–54 — Раскладка плитки л. 56 — Ведомость отделки помещений	акт контрольного обмера	Вопроса в реестре нет: Альбом принимает стены ровными и вертикальными без замера. Результат принимает: Отделочник

Допущения и предложения на листе

Основа листа: размеры сняты с плана заказчика, контрольный обмер не выполнен (К-5); высота потолка 2700 мм принята: на плане заказчика не указана (К-5); подрайон климата не задан — принят не северный (жилые от 2,5 м) (К-4); толщины стен приняты: наружные 250 мм, перегородки 120 мм — не обмерены (К-5); разрешённая мощность 15 кВт принята по типовой квартире, технических условий нет (К-6).

См. лист открытых вопросов (лист 6, записи К-4–К-6).

Изм.	Кол.уч	Лист	№ док.	Подп.	Дата
Разраб.		Кырлан А.С.			14.11.26
Пров.					
ГИП					
Н. контр.					
Утв.					

ГД-2026-006-АИ

Квартира 58 м²

Общая площадь 55,23* м² · * размеры приняты, не замерены (реестр — л. 6, 7, К-5)

Дизайн-проект интерьера

Стадия	Лист	Листов
РП	9	108

Задание на контрольный обмер и обследование.
Лист 2 из 3
М б/м

Кырлан Александр Сергеевич

выпуск 14.11.2026 № bceе049e32 · стр. 9 из 128

Задание на контрольный обмер и обследование. Лист 3 из 3

ПРЕДВАРИТЕЛЬНО · не для производства работ · открыто пунктов: 9 (реестр — л. 6, 7)

Что замерить, вскрыть и получить до заказа материалов и изделий

Документы и данные закупки (не на объекте)

№	У кого, откуда	Способ	Что получить	К какому сроку	Что пересчитается в альбоме	Чем подтверждается	Закрывает вопросы реестра
О-10	адрес объекта, СП 131.13330	Документ	Климатический подрайон по СП 131.13330 (по адресу объекта)	до заказа каркаса потолков	план потолков, разрезы, ведомость объёмов Листы: л. 48 — План потолков	копия документа	К-4 Результат принимает: Архитектор
О-11	заказчик; организация, выдавшая технические условия	Документ	Технические условия на присоединение: разрешённая мощность (принято 15 кВт по типовой квартире).	до утверждения однолинейной схемы щита	однолинейная схема щита: вводной аппарат и группы Листы: л. 32 — Однолинейная схема щита	копия документа	К-6 Результат принимает: Инженер-электрик
О-12	паспорт модели	Документ	Модель стиральной машины: габарит (ширина 600, глубина ≤ 450, высота ≤ 850 под столешницу), тип загрузки, положение подвода и слива	до заказа кухни	ниша М11** кухни, выводы В1/К1, розетка Листы: л. 38 — План выводов сантехники л. 24 — План расстановки мебели л. 32 — Однолинейная схема щита	копия документа	К-7 Результат принимает: Инженер ВК (вода, канализация)
О-13	Поставщик изделий; Спальня (пом. 2)	Закупка	Паспорт или монтажная схема выбранной модели: КВ-2* допустимая длина трассы фреона (минимальная и максимальная), перепад высот между блоками, место наружного блока. Принято в проекте: длина петли принята по типовому минимуму 3 м; паспорта выбранной модели нет.	До закрытия трасс и разводки	Габариты и положение изделий на планах и развёртках, выводы (вода, слив, электро), монтажные зазоры; знак «*» у марки снимается паспортом или чертежом. Листы: л. 24 — План расстановки мебели	паспорт изделия или партии	Вопроса в реестре нет Результат принимает: Инженер ОВ

Примечания

1. Подтверждение: акт контрольного обмера (дата, кто присутствовал, прибор, перечень промеров с результатами, подписи присутствующих); к акту — фото вскрытий и узлов и техническое заключение организации, выполнившей обследование.
2. Номера листов — по ведомости рабочих чертежей комплекта (лист «Общие данные»).
3. Пункт исключается из задания при следующем выпуске, когда акт подписан, значение внесено в проект и листы перевыпущены; знак «*» у величины снимается только замером.

Допущения и предложения на листе

Основа листа: размеры сняты с плана заказчика, контрольный обмер не выполнен (К-5); высота потолка 2700 мм принята: на плане заказчика не указана (К-5); подрайон климата не задан — принят не северный (жилые от 2,5 м) (К-4); толщины стен приняты: наружные 250 мм, перегородки 120 мм — не обмерены (К-5); разрешённая мощность 15 кВт принята по типовой квартире, технических условий нет (К-6).

Знак «*» — принято, не замерено и не подтверждено (замерить на объекте): ИЗ-4: КВ-2 — длина петли принята по типовому минимуму 3 м; паспорта выбранной модели нет.

Знак «**» — предложение проектировщика, заказчиком не утверждено (согласовать с заказчиком): К-7: М11 — место стиральной машины: вместо модуля с ящиками 400 справа от варочной; ряд до 3420, журнальный стол М21 (с х 3440) не мешает загрузке.

См. лист открытых вопросов (лист 6, записи К-4–К-7; лист 7, запись ИЗ-4).

Изм.	Кол.уч	Лист	№ док.	Подп.	Дата
Разраб.		Кырлан А.С.			14.11.26
Пров.					
ГИП					
Н. контр.					
Утв.					

ГД-2026-006-АИ

Квартира 58 м²

Общая площадь 55,23* м² · * размеры приняты, не замерены (реестр — л. 6, 7, К-5)

Дизайн-проект интерьера

Стадия	Лист	Листов
РП	10	108

Задание на контрольный обмер и обследование.
Лист 3 из 3
М б/м

Кырлан Александр Сергеевич

выпуск 14.11.2026 № bcee049e32 · стр. 10 из 128

График закупок и работ. Лист 1 из 3

ПРЕДВАРИТЕЛЬНО · не для производства работ · открыто пунктов: 9 (реестр — л. 6, 7)

Что заказывать и когда не раньше чего: относительный порядок без дат; срок поставки — из данных или «не задан» с записью реестра

Лист не содержит дат: контрольного обмера, подписанных решений автора и договоров ещё нет, и любая дата была бы выдумана. Вместо календаря — порядок и условия: замер → решение и выбор изделия → заказ → срок поставки → работа, которую позиция блокирует.
Срок поставки печатается как срок, только если он задан в данных позиции. Нет — «срок поставки не задан» и ссылка на вопрос реестра о сроках; типовой диапазон практики стоит рядом как ориентир и заказывать по нему нельзя. Номера З-N и Р-N — строки этого листа, К-N — записи реестра открытых вопросов, О-N — позиции задания на контрольный обмер.

Закупки: что заказывается, от чего зависит заказ и какую работу блокирует

№	Позиция и где	1. Замер до заказа	2. Решение, выбор изделия, паспорт	3. Условие заказа	4. Срок поставки	5. Блокирует работу	Закрывает вопросы реестра
З-1	Двери скрытого монтажа с коробом под покраску в существующих проёмах: Д-2, Д-3, Д-4 — 5 шт. пом. 5, 6	О-7: обмер: все помещения квартиры (К-5); до заказа мебели, дверей и каркаса потолков		После 1 и 2 и после получения срока у поставщика (вопроса о сроках нет); дата заказа — когда срок известен, не позднее чем за срок до начала Р-5.	срок поставки не задан (записи реестра нет) Ориентир практики (не срок поставщика): ≈ 30 дн.	Р-5 «штукатурка»: короб ставят до штукатурки (коробку ставят на черновой стадии; полотно навешивают после чистовой отделки стен)	К-5
З-2	Кухонный гарнитур по проекту кухни: модули М4, М5, М6, М7, М11**, М8, М10 пом. 1			После 1 и 2 и после получения срока у поставщика (вопроса о сроках нет); дата заказа — когда срок известен, не позднее чем за срок до начала Р-15.	срок поставки не задан (записи реестра нет) Ориентир практики (не срок поставщика): 4–8 нед. от замера	Р-15 «кухня и мебель»: замер кухни — по готовым стенам после штукатурки или плитки, до чистового пола; производство идёт параллельно со стяжкой и отделкой	
З-3	Встраиваемая техника кухни: М4 холодильник, М11** washer пом. 1			После 1 и 2 и после получения срока у поставщика (вопроса о сроках нет); дата заказа — когда срок известен, не позднее чем за срок до начала Р-15.	срок поставки не задан (записи реестра нет)	Р-15 «кухня и мебель»: паспорта и монтажные схемы — до изготовления модулей кухни: нишу и вентзазоры задаёт модель, а не типовая схема 60 см	
З-4	Стиральная машина: П6** (вертикальная загрузка 400 × 600 мм — условие закупки) пом. 1		О-12: Модель стиральной машины: габарит (ширина 600, глубина ≤ 450, высота ≤ 850 под столешницу), тип загрузки, положение подвода и слива (К-7); до заказа кухни	После 1 и 2 и после получения срока у поставщика (вопроса о сроках нет); дата заказа — когда срок известен, не позднее чем за срок до начала Р-4.	срок поставки не задан (записи реестра нет)	Р-4 «черновая сантехника»: габарит и подводка — до закрытия люка и разводки	К-7
З-5	Сантехнические приборы и инсталляции: П4, П1**, П3**, П20 пом. 1, 3, 4	О-3: обмер: у окон		После 1 и 2 и после получения срока у поставщика (вопроса о сроках нет); дата заказа — когда срок известен, не позднее чем за срок до начала Р-4.	срок поставки не задан (записи реестра нет)	Р-4 «черновая сантехника»: инсталляцию ставят до обшивки ГКЛВ и до гидроизоляции стены	
З-6	Керамогранит и плитка: 2 поз. по артикулу и формату, 46,11 м² по раскладке пом. 3, 4, 5	О-8: обмер: Кухня-гостиная (пом. 1), Спальня (пом. 2), Ванная (пом. 3), Санузел (пом. 4), Прихожая (пом. 5), Гардеробная (пом. 6) О-9: обмер: Кухня-гостиная (пом. 1), Спальня (пом. 2), Ванная (пом. 3), Санузел (пом. 4), Прихожая (пом. 5), Гардеробная (пом. 6)		После 1 и 2 и после получения срока у поставщика (вопроса о сроках нет); дата заказа — когда срок известен, не позднее чем за срок до начала Р-9.	срок поставки не задан (записи реестра нет)	Р-9 «плитка»: калибр партии измеряют до раскладки, раскладку пересчитывают до заказа	

Допущения и предложения на листе

Основа листа: размеры сняты с плана заказчика, контрольный обмер не выполнен (К-5); высота потолка 2700 мм принята: на плане заказчика не указана (К-5); подрайон климата не задан — принят не северный (жилые от 2,5 м) (К-4); толщины стен приняты: наружные 250 мм, перегородки 120 мм — не обмерены (К-5); разрешённая мощность 15 кВт принята по типовой квартире, технических условий нет (К-6).
Знак «**» — предложение проектировщика, заказчиком не утверждено (согласовать с заказчиком): К-2: П1 — ванна 1500 вместо 1600 — не заходит в проход перед проёмом Д-4; перед ванной 680 мм — глубина помещения; П3 — умывальник у стены В справа от ванны — перед ним свободно 750 мм, до стены Б 90 мм; К-7: М11 — место стиральной машины: вместо модуля с ящиками 400 справа от варочной; ряд до 3420, журнальный стол М21 (с х 3440) не мешает загрузке; П6 — стиральная машина на кухне: в ванной и санузле места нет; подвод ХВС с шаровым краном, слив — встраиваемый сифон с обратным клапаном (водяной затвор), отдельная группа 6 щита с УЗО 30 мА.
См. лист открытых вопросов (лист 6, записи К-2, К-4–К-7).

Изм.	Кол.уч	Лист	№ док.	Подп.	Дата
Разраб.		Кырлан А.С.			14.11.26
Пров.					
ГИП					
Н. контр.					
Утв.					

ГД-2026-006-АИ

Квартира 58 м²

Общая площадь 55,23* м² · * размеры приняты, не замерены (реестр — л. 6, 7, К-5)

Дизайн-проект интерьера

Стадия	Лист	Листов
РП	11	108

График закупок и работ. Лист 1 из 3

М б/м

Кырлан Александр Сергеевич

выпуск 14.11.2026 bcee049e32 · стр. 11 из 128

График закупок и работ. Лист 2 из 3

Что заказывать и когда не раньше чего: относительный порядок без дат; срок поставки — из данных или «не задан» с записью реестра

Закупки: что заказывается, от чего зависит заказ и какую работу блокирует (продолжение)

№	Позиция и где	1. Замер до заказа	2. Решение, выбор изделия, паспорт	3. Условие заказа	4. Срок поставки	5. Блокирует работу	Закрывает вопросы реестра
З-7	Покрытие пола (доска) и плинтус: пом. 1, 2, 6 пом. 1, 2, 6	О-8: обмер: Кухня-гостиная (пом. 1), Спальня (пом. 2), Ванная (пом. 3), Санузел (пом. 4), Прихожая (пом. 5), Гардеробная (пом. 6)		После 1 и 2 и после получения срока у поставщика (вопроса о сроках нет); дата заказа — когда срок известен, не позднее чем за срок до начала Р-12.	срок поставки не задан (записи реестра нет)	Р-12 «чистовые полы»: артикул и партия — до заказа; доску привозят к чистовым полам	
З-8	Встроенная мебель по замеру цеха: М9 пом. 5	О-7: обмер: все помещения квартиры (К-5); до заказа мебели, дверей и каркаса потолков		После 1 и 2 и после получения срока у поставщика (вопроса о сроках нет); дата заказа — когда срок известен, не позднее чем за срок до начала Р-15.	срок поставки не задан (записи реестра нет) Ориентир практики (не срок поставщика): 4–8 нед. от замера	Р-15 «кухня и мебель»: цех замеряет по готовым стенам; производство 4–8 недель идёт параллельно с отделкой	К-5

Работы: порядок и что не даёт начать

№	Работа (стадия технологической последовательности)	После	Что должно быть к началу: условия и закупки	Не начинать, пока открыто в реестре
Р-1	Демонтаж покрытий, отделки стен и потолков, дверных блоков и приборов; конструкции, стены и перегородки не трогать до технического заключения (стадия 1)		до начала: запрошены документы на дом и БТИ; контрольный обмер до демонтажа (что видно) сделан	
Р-2	Контрольный обмер на голых стенах и обследование (задание — лист «Задание на контрольный обмер») (стадия 2)	Р-1	после снятия отделки: видны стояки, каналы, щиток, толщины стен; до заказа всего, что делают по размеру	
Р-3	Черновая электрика: штробы, короба, гофра, подрозетники, щит (стадия 4)	Р-2	до начала: план электрики с высотами утверждён; штробы в стенах — только после технического заключения; мебель расставлена	К-6: Разрешённая мощность 15 кВт принята по типовой квартире, технических условий в материалах объекта нет.
Р-4	Черновая сантехника и вентиляция: разводка, выводы, инсталляции, короба стояков (стадия 5)	Р-2	до начала: положение стояков замерено; модели инсталляций и машины выбраны (габариты рамы, подводка); инсталляцию ставят до обшивки ГКЛВ и до гидроизоляции Закупки к началу: З-4 (стиральная машина), З-5 (сантехника)	К-7: Места стиральной машины в квартире не было.
Р-5	Коробки скрытых дверей, затем штукатурка стен и откосов (стадия 6)	Р-2, Р-3, Р-4	до начала: электрика и сантехника смонтированы, штробы заделаны; коробки скрытых дверей установлены до штукатурки (поэтому заказ дверей — раньше работы) Закупки к началу: З-1 (двери скрытого монтажа)	К-5: Основа альбома — план заказчика без контрольного обмера: размеры помещений сняты с плана, высота потолка 2700 мм и толщины стен (наружные 250 мм, перегородки 120 мм) приняты — на плане они не указаны.
Р-6	Стяжка пола и тёплый пол (стадия 7)	Р-5	до начала: штукатурка сделана; трубы под стяжкой приняты; нивелировка плиты выполнена	

Допущения и предложения на листе

Основа листа: размеры сняты с плана заказчика, контрольный обмер не выполнен (К-5); высота потолка 2700 мм принята: на плане заказчика не указана (К-5); подрайон климата не задан — принят не северный (жилые от 2,5 м) (К-4); толщины стен приняты: наружные 250 мм, перегородки 120 мм — не обмерены (К-5); разрешённая мощность 15 кВт принята по типовой квартире, технических условий нет (К-6).

См. лист открытых вопросов (лист 6, записи К-4–К-6).

Изм.	Кол.уч	Лист	№ док.	Подп.	Дата	ГД-2026-006-АИ			
						Квартира 58 м²			
						Общая площадь 55,23* м² · * размеры приняты, не замерены (реестр — л. 6, 7, К-5)			
Разраб.		Кырлан А.С.			14.11.26	Дизайн-проект интерьера	Стадия	Лист	Листов
Пров.							РП	12	108
ГИП									
Н. контр.						**График закупок и работ. Лист 2 из 3** М б/м	**Кырлан Александр Сергеевич**		
Утв.									

выпуск 14.11.2026 № bcee049e32 · стр. 12 из 128

График закупок и работ. Лист 3 из 3

Что заказывать и когда не раньше чего: относительный порядок без дат; срок поставки — из данных или «не задан» с записью реестра

Работы: порядок и что не даёт начать (продолжение)

№	Работа (стадия технологической последовательности)	После	Что должно быть к началу: условия и закупки	Не начинать, пока открыто в реестре
Р-7	Гидроизоляция санузлов и тест проливом (стадия 8)	Р-6	до начала: стяжка набрала прочность и сухая по инструкции гидроизоляции; выводы стоят на проектных отметках	
Р-8	ГКЛ: короба инсталляции и стояков, ниши, потолки (стадия 9)	Р-3, Р-4	до начала: черновые сети в зоне коробов приняты; закладные под тяжёлое и карнизы стоят; светильники выбраны (вырезы)	
Р-9	Плитка и керамогранит: стены, затем пол; фартук (стадия 10)	Р-6, Р-7, Р-8	до начала: гидроизоляция принята; плитка выбрана, калибр партии измерен, раскладка пересчитана и подписана Закупки к началу: З-6 (плитка)	
Р-10	Шпаклёвка стен и потолков под окраску (стадия 11)	Р-5, Р-8, Р-9	до начала: плитка готова (грязные работы закончены); штукатурка и ГКЛ сухие	
Р-11	Окраска стен, потолков, откосов (стадия 13)	Р-10	до начала: шпаклёвка отшлифована и огрунтована; выкрасы утверждены, колеровка одной партией	
Р-12	Чистовые полы: инженерная доска (стадия 14)	Р-9, Р-11	до начала: влажность основания в норме, мокрые работы закончены; доска выбрана и привезена Закупки к началу: З-7 (доска и плинтус)	
Р-13	Полотна межкомнатных дверей, плинтусы, пороги (стадия 15)	Р-11, Р-12	до начала: чистовой пол уложен; полотна скрытых дверей — после чистовой отделки стен	
Р-14	Чистовая электрика и сантехника: механизмы, светильники, смесители, приборы (стадия 16)	Р-11, Р-13	до начала: отделка готова; механизмы, светильники и приборы выбраны и привезены	
Р-15	Кухня, встроенная и корпусная мебель, бытовая техника (стадия 17)	Р-13, Р-14	до начала: чистовая сантехника и электрика подведены к местам мебели; замер кухни снят по готовым стенам (после штукатурки или плитки, до чистового пола) Закупки к началу: З-2 (кухонный гарнитур), З-3 (техника кухни), З-8 (мебель по замеру)	К-5: Основа альбома — план заказчика без контрольного обмера: размеры помещений сняты с плана, высота потолка 2700 мм и толщины стен (наружные 250 мм, перегородки 120 мм) приняты — на плане они не указаны.
Р-16	Сдача: осмотр по чек-листу, дефектная ведомость, устранение замечаний (стадия 18)	Р-14, Р-15	до начала: всё смонтировано; акты скрытых работ подписаны	

Примечания

1. Порядок работ — стадии технологической последовательности из 16 позиций, присутствующих в этом проекте (по строкам ведомости объёмов); остальные стадии таблицы knowledge/remont-tehnologiya.md в проекте не встречаются. Длительности работ не печатаются: их нет ни в данных, ни в нормах для этого объекта.
2. Типовые сроки — ориентир практики, не срок поставщика: скрытые двери — короб около 10 дн., полотно под покраску до 3 нед., шпон 4–5 нед., в среднем около 30 дн. (knowledge/workers/foreman.md, п. 2.4 (profil-doors)); кухня и корпусная мебель — 4–8 недель от замера (knowledge/remont-tehnologiya.md, разд. 2; knowledge/workers/foreman.md, п. 2.4). Заказ по ориентиру не назначается: срок получают у поставщика (вопрос реестра), после чего заказ планируют «не позднее чем за срок до начала работы».
3. Условия заказа берутся из реестра открытых вопросов и задания на контрольный обмер: позиция заказывается, когда закрыты замер (графа 1) и решение (графа 2). Закрывать их может только факт или решение автора с подписью; снять строку с листа можно только закрыв запись реестра.
4. Заказ по размеру до контрольного обмера не делают: двери, кухня и встроенная мебель зависят от обмера (К-11, К-13); скрытые двери, кроме того, зависят от решения по нише санузла 2 (проём Д-5 в перегородке П-1).
5. Номера листов — по ведомости рабочих чертежей комплекта (лист «Общие данные»).

Допущения и предложения на листе

Основа листа: размеры сняты с плана заказчика, контрольный обмер не выполнен (К-5); высота потолка 2700 мм принята: на плане заказчика не указана (К-5); подрайон климата не задан — принят не северный (жилые от 2,5 м) (К-4); толщины стен приняты: наружные 250 мм, перегородки 120 мм — не обмерены (К-5); разрешённая мощность 15 кВт принята по типовой квартире, технических условий нет (К-6).
См. лист открытых вопросов (лист 6, записи К-4–К-6).

Изм.	Кол.уч	Лист	№ док.	Подп.	Дата
Разраб.		Кырлан А.С.			14.11.26
Пров.					
ГИП					
Н. контр.					
Утв.					

ГД-2026-006-АИ

Квартира 58 м²

Общая площадь 55,23* м² · * размеры приняты, не замерены (реестр — л. 6, 7, К-5)

Дизайн-проект интерьера

Стадия	Лист	Листов
РП	13	108

График закупок и работ. Лист 3 из 3

М б/м


Кырлан Александр Сергеевич

Календарный график работ и закупок

ПРЕДВАРИТЕЛЬНО · не для производства работ · открыто пунктов: 9 (реестр — л. 6, 7)

Недели, зависимости, техпаузы и даты заказа длинных позиций · длительности — ориентир по таблице типовых сроков, не обещание бригады

№	Работа	Нед.	После
Р-1	**демонтаж**	1	
Р-2	**контрольный обмер**	0,5	Р-1
Р-3	**черновая электрика**	1,25	Р-2
Р-4	черновая сантехника	1	Р-2
Р-5	**штукатурка**	2	Р-3, Р-4
Р-6	**стяжка**	0,75	Р-5
Р-7	**гидроизоляция**	0,5	Р-6
Р-8	ГКЛ	1,25	Р-3, Р-4
Р-9	**плитка**	2,5	Р-7, Р-8, Р-6
Р-10	**шпаклёвка**	2,25	Р-9, Р-8, Р-5
Р-11	**окраска**	1,75	Р-10
Р-12	**чистовые полы**	1	Р-11, Р-9
Р-13	**двери и плинтусы**	0,75	Р-12, Р-11
Р-14	**чистовая электрика и сантехника**	0,75	Р-13, Р-11
Р-15	**кухня и мебель**	0,75	Р-14, Р-13
Р-16	**сдача**	0,5	Р-15, Р-14
Закупки: заказать не позднее — «◆»; от заказа до поставки — штриховая полоса; срок поставки — только из данных или «ориентир практики»			
З-1	Двери скрытого монтажа с коробом под покраску в существующих проёмах: Д-2, Д-3, Д-4 — 5 шт	4,25	для Р-5
З-2	Кухонный гарнитур по проекту кухни: модули М4, М5, М6, М7, М11**, М8, М10	6	для Р-15
З-3	Встраиваемая техника кухни: М4 холодильник, М11** стиральная машина		для Р-15
З-4	Стиральная машина: П6** (вертикальная загрузка 400 × 600 мм — условие закупки)		для Р-4
З-5	Сантехнические приборы и инсталляции: П4, П1**, П3**, П20		для Р-4
З-6	Керамогранит и плитка: 2 поз. по артикулу и формату, 46,11 м² по раскладке		для Р-9
З-7	Покрытие пола (доска) и плинтус: пом. 1, 2, 6		для Р-12
З-8	Встроенная мебель по замеру цеха: М9	6	для Р-15

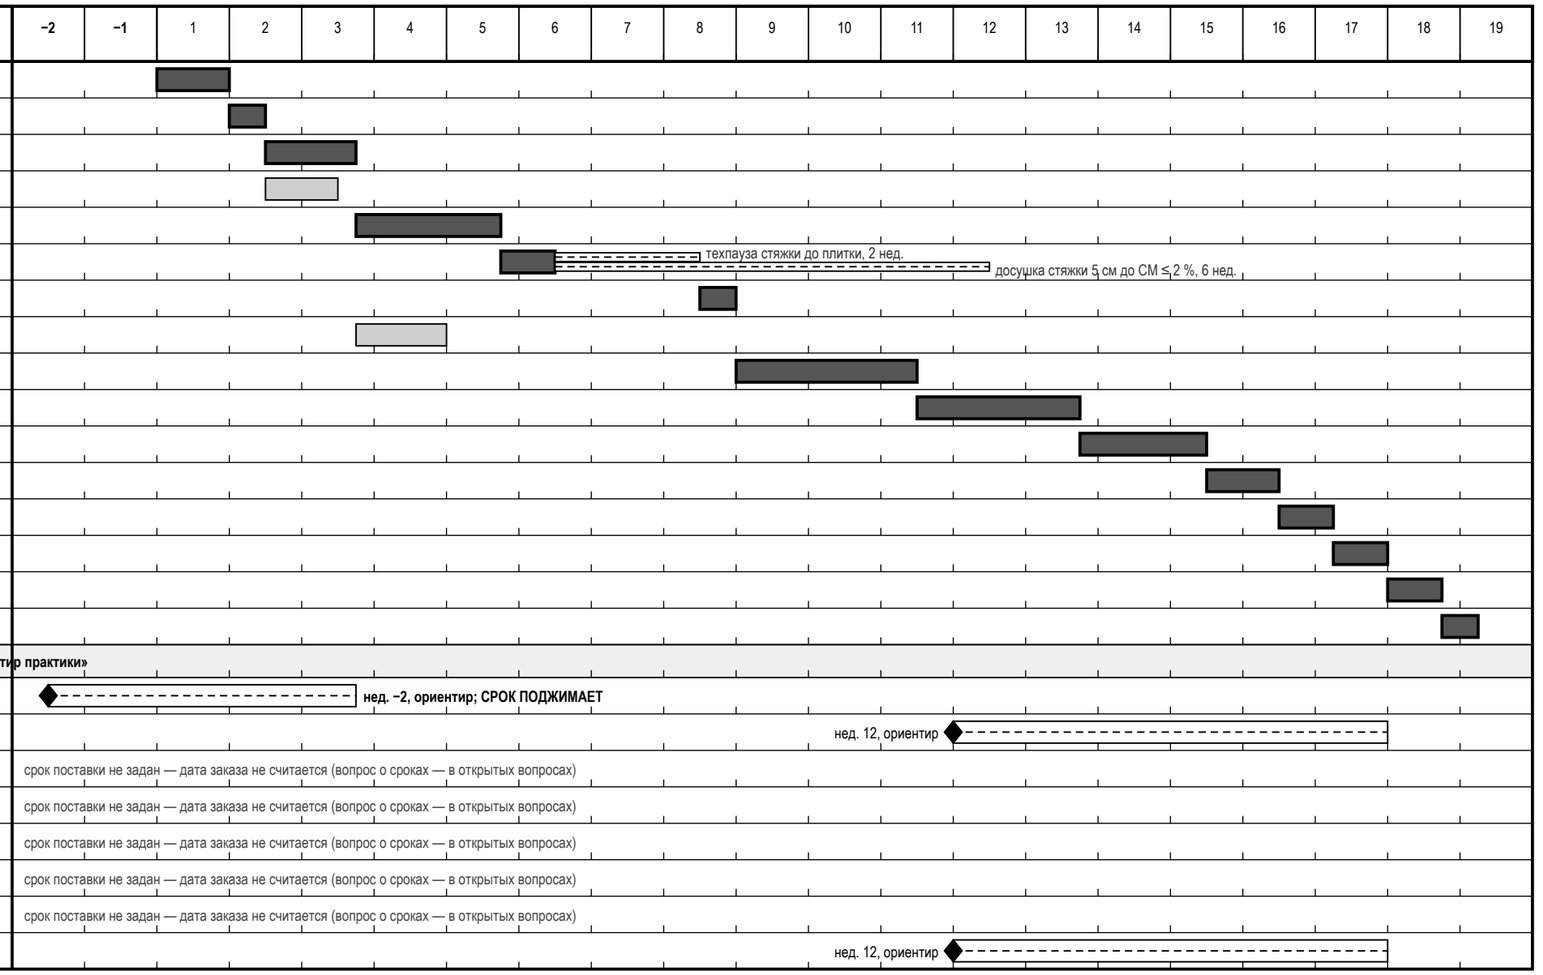

Итого: ≈ 18,25 нед. · жирная линия и тёмная полоса — критический путь

Примечания

1. Длительности этапов — типовые сроки по площади 55,23 м² (таблица «Свод для графика»: недели по этапам для 45, 80 и 120 м², середина вилки, линейная интерполяция); это ориентир, а не норма и не обещание бригады. Контрольный обмер — ориентир 0,5 нед. (в таблице нет).
2. Зависимости «после» — из графика закупок и работ (лист «График закупок и работ»); каждая работа начинается после конца предшественников. Техпаузы стоят отдельными полосами, а не спрятаны в длительности: стяжка → плитка — не менее 2 нед.; стяжка → чистовой пол — досушка стяжки 5 см до СМ ≤ 2 % — 6 нед. (ориентир «1 нед. на 1 см до 4 см, 5 см — 6 нед., 6 см — 8 нед.»; решает замер).
3. График последовательный и поэтому консервативный: в жизни шпаклёвка, плитка и досушка стяжки идут частично параллельно (таблица типовых сроков для 55,23 м²: 13–16 нед.). Совмещения — решение прораба после обмера.
4. Закупки: «заказать не позднее» = начало работы, которой нужна позиция, минус срок поставки. Срок поставки — из данных проекта (срок поставки позиции, срок изготовления обоев в отделке); если его нет, в графике стоит типовой диапазон практики с пометкой «ориентир» — это не срок поставщика, его надо получить до заказа. Кухню и встроенную мебель заказывают после замера по готовым стенам (после штукатурки). Позиции без срока дат заказа не имеют.
5. «Срок поджимает»: самая поздняя дата заказа раньше, чем позицию можно заказать (до замера или обмера): сдвиньте начало работ, ищите изделие с меньшим сроком или заказывайте по предварительному размеру — решение прораба и заказчика.

Допущения и предложения на листе

Основа листа: размеры сняты с плана заказчика, контрольный обмер не выполнен (К-5); высота потолка 2700 мм принята: на плане заказчика не указана (К-5); подрайон климата не задан — принят не северный (жилые от 2,5 м) (К-4); толщины стен приняты: наружные 250 мм, перегородки 120 мм — не обмерены (К-5); разрешённая мощность 15 кВт принята по типовой квартире, технических условий нет (К-6).

Знак «**» — предложение проектировщика, заказчиком не утверждено (согласовать с заказчиком): К-2: П1 — ванна 1500 вместо 1600 — не заходит в проход перед проёмом Д-4; перед ванной 680 мм — глубина помещения; П3 — умывальник у стены В справа от ванны — перед ним свободно 750 мм, до стены Б 90 мм; К-7: М11 — место стиральной машины: вместо модуля с ящиками 400 справа от варочной; ряд до 3420, журнальный стол М21 (с х 3440) не мешает загрузке; П6 — стиральная машина на кухне: в ванной и санузле места нет; подвод ХВС с шаровым краном, слив — встраиваемый сифон с обратным клапаном (водяной затвор), отдельная группа 6 щита с УЗО 30 мА.

См. лист открытых вопросов (лист 6, записи К-2, К-4–К-7).

Изм.	Кол.уч	Лист	№ док.	Подп.	Дата
Разраб.		Кырлан А.С.			14.11.26
Пров.					
ГИП					
Н. контр.					
Утв.					

ГД-2026-006-АИ

Квартира 58 м²

Общая площадь 55,23* м² · * размеры приняты, не замерены (реестр — л. 6, 7, К-5)

Дизайн-проект интерьера	Стадия	Лист	Листов
	РП	14	108
Календарный график работ и закупок М б/м	**Кырлан Александр Сергеевич**		

Чек-лист приёмки по этапам. Лист 1 из 4

По этапам Р-1…Р-N: что проверить, чем, какой допуск и какой акт подписать до закрытия работы

ПРЕДВАРИТЕЛЬНО · не для производства работ · открыто пунктов: 9 (реестр — л. 6, 7)

Приёмка по этапам: контрольные точки, допуски и акты скрытых работ

Этап	Контрольная точка (дальше не пускают без подписи)	Что проверяют	Чем	Допуск	Основание	Подпись	Акт скрытых работ / документ
Р-1	Демонтаж До начала демонтажа: запрошены документы на дом и БТИ	Что снимается и что не трогается: покрытия, отделка, дверные блоки; несущие стены и перегородки — без изменений	осмотр по плану демонтажа	снятое — только по плану; несущее не затрагивать	практика		Фото помещений до и после демонтажа; перечень снятого в журнале работ.
Р-2	Контрольный обмер Контрольный обмер на голых стенах сделан до заказа всего, что делают по размеру	Размеры помещений и проёмов, диагонали, положение стояков, щитка, каналов, толщины стен	рулетка, лазерный дальномер, уровень	допуск задаёт проект; расхождение с планом — в перечень открытых вопросов до заказа	практика		Протокол контрольного обмера с эскизом; расхождения занесены в открытые вопросы.
Р-3	Черновая электрика Черновая электрика: трассы, высоты подрозетников, замер изоляции подписаны до заделки	Сопротивление изоляции проводки (цепи до 1000 В)	мегаомметр	не менее 0,5 МОм	норматив (ПУЭ, гл. 1.8)		Акт скрытых работ на трассы проводки и слаботочные линии до закрытия штукатуркой и ГКЛ; исполнительная схема трасс с привязками; заземление и уравнивание потенциалов в санузле протокол и фото.
		Целостность и маркировка: PE жёлто-зелёный, N — синий, L — прочие цвета	визуально, прозвонка	каждый проводник промаркирован	практика		
		Высоты подрозетников и привязки — по плану розеток и выключателей	рулетка, уровень	по проекту; от чистого пола	практика		
Р-4	Черновая сантехника Черновая сантехника: опрессовка, отметки выводов, инсталляции подписаны до зашивки	Опрессовка водоснабжения: рабочее давление до 0,6 МПа — испытание 0,9 МПа; выше 0,6 МПа — по расчёту	опрессовочный насос, манометр	выдержка 10 мин (поквартирная); падение: пластик не более 0,06 МПа за 30 мин, сталь не более 0,05 МПа за 10 мин	практика (СП 73.13330)		Акт опрессовки (давление, время, результат); акт скрытых работ на трассы в стенах, полу и коробах; инсталляции, скрытые смесители, трапы — фото с рулеткой и отметками.
		Уклон канализации Ø40–50	уровень, построитель плоскостей	не менее 20 мм на 1 м	норматив (СП 30.13330)		
		Протечки в соединениях, сифоны, смесители, гибкая подводка	осмотр под давлением, салфетка на стыках	нет капель и влажных следов в контрольное время	практика		
		Отметки выводов и положение инсталляций до зашивки и гидроизоляции	рулетка в кадре, фото	по листу выводов	практика		
Р-5	Штукатурка Маяки стен проверены до штукатурки; коробки скрытых дверей стоят до штукатурки	Отклонение от вертикали (простая / улучшенная / высококачественная штукатурка)	отвес, лазерный уровень	3 / 2 / 1 мм на 1 м; не более 15 / 10 / 5 мм на высоту	практика (СП 71.13330.2017)		Фото коробок скрытых дверей с отметкой чистого пола — до штукатурки; класс штукатурки (простая / улучшенная / высококачественная) назван в договоре.
		Отклонение от горизонтали	уровень, правило	3 / 2 / 1 мм на 1 м; не более 15 / 10 / 5 мм на длину	практика (СП 71.13330.2017)		

Допущения и предложения на листе

Основа листа: размеры сняты с плана заказчика, контрольный обмер не выполнен (К-5); высота потолка 2700 мм принята: на плане заказчика не указана (К-5); подрайон климата не задан — принят не северный (жилые от 2,5 м) (К-4); толщины стен приняты: наружные 250 мм, перегородки 120 мм — не обмерены (К-5); разрешённая мощность 15 кВт принята по типовой квартире, технических условий нет (К-6).

См. лист открытых вопросов (лист 6, записи К-4–К-6).

Изм.	Кол.уч	Лист	№ док.	Подп.	Дата
Разраб.		Кырлан А.С.			14.11.26
Пров.					
ГИП					
Н. контр.					
Утв.					

ГД-2026-006-АИ

Квартира 58 м²

Общая площадь 55,23* м² · * размеры приняты, не замерены (реестр — л. 6, 7, К-5)

Дизайн-проект интерьера

Стадия	Лист	Листов
РП	15	108

Чек-лист приёмки по этапам. Лист 1 из 4

М б/м

Кырлан Александр Сергеевич

выпуск 14.11.2026 № bcee049e32 · стр. 15 из 128

Чек-лист приёмки по этапам. Лист 2 из 4

По этапам Р-1…Р-N: что проверить, чем, какой допуск и какой акт подписать до закрытия работы

Приёмка по этапам: контрольные точки, допуски и акты скрытых работ (продолжение)

Этап	Контрольная точка (дальше не пускают без подписи)	Что проверяют	Чем	Допуск	Основание	Подпись	Акт скрытых работ / документ
		Неровности (плоскостность)	правило 2 м и щуп	до 5 / 3 / 2 мм на 1 м; не более 3 / 2 / 2 неровностей на 4 м²	практика (СП 71.13330.2017)		
		Влажность основания перед шпаклёвкой и отделкой	влагомер	верхние 20–30 мм — не более 5 % по массе	норматив (СП 71, табл. 7.2)		
Р-6	Стяжка Стяжка: подготовка, после заливки ровность, затем замер СМ перед чистовым полом	Ровность: просвет под рейкой 2 м	рейка 2 м, клиновой щуп	под паркет, ламинат — 2 мм; под гидроизоляцию до 4 мм; прочие покрытия — до 6 мм (цифры расходятся между источниками — сверить перед актом)	практика (СП 29.13330)		Акт скрытых работ на стяжку (толщина, армирование) до чистового пола; протокол ровности и протокол СМ-влажности; звукоизоляция и демпферная лента под стяжкой — фото и паспорт; контуры тёплого пола до заливки — схема укладки и замер сопротивления.
		Отклонение от горизонтали по помещению	уровень, нивелир	не более 0,2 % длины помещения	практика (СП 29.13330)		
		Число точек измерения	рейка	не менее 3 на 30 м² или 1 на небольшое помещение	практика		
		Отслоения и пустоты	простукивание молотком или киянкой	глухой звук — зона вскрывается и переделывается	практика		
		Влажность перед укладкой доски: цементная стяжка	влагомер; СМ-замер	ЦПС не более 2,0 % СМ (с тёплым полом не более 1,8 %); влагомер для плитки — не более 5 %	практика (СП 71; рекомендации производителей)		
Р-7	Гидроизоляция Гидроизоляция: пролив 24 ч подпись до плитки	Заведение на стены не ниже 200 мм от чистого пола; за ванной — 300 мм выше борта; в душе без поддона — на высоту лейки	рулетка	не менее 200 мм	норматив (СП 71.13330.2017, п. 8.6.5); остальное — практика		Акт теста проливом, фото узлов и высоты заведения на стены — до плитки.
		Тест проливом: слой воды 10–30 мм, контроль уровня и потолка соседа снизу	линейка, визуально	24 ч (минимум 12 ч); падения уровня и протечки нет	практика		
		Два слоя обмазки с межслойной сушкой, лента в углах и манжеты на выводах	визуально	по инструкции производителя	практика		
Р-8	ГКЛ Короба, ниши и потолки: черновые сети в зоне коробов приняты до обшивки	Шаг саморезов, отступ от кромки, заделка стыков (как у перегородок)	рулетка, визуально	потолок 150 мм; кромка 5–10 мм; стык — лента и 2 слоя шпаклёвки	практика (СП 163.1325800.2014)		Акт скрытых работ: каркас ГКЛ, закладные, звукоизоляция — фото до обшивки; воздуховоды в коробах и за потолком — фото и схема.
		Закладные под тяжёлое, карнизы, подвесные светильники на месте до обшивки	фото с привязками	по плану потолков и узлам	практика		
		Ревизионные люки: доступ к арматуре и ревизиям сохранён	осмотр	по листу ВК	практика		

Допущения и предложения на листе

Основа листа: размеры сняты с плана заказчика, контрольный обмер не выполнен (К-5); высота потолка 2700 мм принята: на плане заказчика не указана (К-5); подрайон климата не задан — принят не северный (жилые от 2,5 м) (К-4); толщины стен приняты: наружные 250 мм, перегородки 120 мм — не обмерены (К-5); разрешённая мощность 15 кВт принята по типовой квартире, технических условий нет (К-6).

См. лист открытых вопросов (лист 6, записи К-4–К-6).

Изм.	Кол.уч	Лист	№ док.	Подп.	Дата
Разраб.		Кырлан А.С.			14.11.26
Пров.					
ГИП					
Н. контр.					
Утв.					

ГД-2026-006-АИ

Квартира 58 м²

Общая площадь 55,23* м² · * размеры приняты, не замерены (реестр — л. 6, 7, К-5)

Дизайн-проект интерьера

Стадия	Лист	Листов
РП	16	108

Чек-лист приёмки по этапам. Лист 2 из 4

М б/м

Кырлан Александр Сергеевич

Чек-лист приёмки по этапам. Лист 3 из 4

По этапам P-1…P-N: что проверить, чем, какой допуск и какой акт подписать до закрытия работы

ПРЕДВАРИТЕЛЬНО · не для производства работ · открыто пунктов: 9 (реестр — л. 6, 7)

Приёмка по этапам: контрольные точки, допуски и акты скрытых работ (продолжение)

Этап	Контрольная точка (дальше не пускают без подписи)	Что проверяют	Чем	Допуск	Основание	Подпись	Акт скрытых работ / документ
P-9	Плитка Раскладка плитки: первая плита и первый ряд проверены по развёртке; плитка выбрана, калибр партии измерен	Уступы между смежными плитками	линейка, на просвет	не более 1 мм	норматив (СП 71.13330.2017)		Раскладка подписана до начала плитки; протокол первого ряда; акт теста проливом приложен (этап гидроизоляции).
		Ширина шва и его прямолинейность	линейка, калибр	до 6 мм ручная укладка; фактическая по проекту ±0,5 мм	практика		
		Отклонение рядов от вертикали и горизонтали	уровень, правило, отвес	1,5 мм на 1 м длины	практика		
		Ровность облицовки	правило 2 м и щуп	не более 2–4 мм (цифра расходится по источникам)	практика		
		Пустоты под плиткой	простукивание всей площади	до 10 % площади допустимо; свыше 25 % под одной плиткой — брак	практика		
P-10	Шпаклёвка Шпаклёвка Q3/Q4: проверка боковым светом до окраски	Класс основания под окраску: Q3 — сплошное финишное шпаклевание; Q4 — под направленный свет	переносной прожектор у поверхности под острым углом	Q3: царапины от абразива до 0,5 мм; Q4 — без видимых царапин и теней; неровность на 2 м: Q3 — 1 мм, Q4 — 0,5 мм	практика (Q-классы — не норматив СП, а согласованный критерий)		Класс (Q3 или Q4) назван в договоре; грунтование и армирование стыков перед шпаклёвкой — запись в журнале.
P-11	Окраска Выкрасы утверждены, колеровка одной партией	Окраска без полос, подтёков, пропусков; цвет — по колерной карте	боковой свет, образец выкраса	без видимых дефектов при боковом свете	практика		Утверждённые выкрасы; остаток колеровки одной партии — для подкраски.
		Основание сухое, огрунтованное; защита от прямого солнца при высыхании	осмотр	по ТУ краски	норматив (СП 71.13330.2017, п. 7.5.2)		
P-12	Чистовые полы Чистовые полы: влажность, ровность, уступы, зазоры — до укладки доски; мокрые работы закончены	Деформационный зазор у стен и порогов (доска, ламинат)	линейка, клинья при укладке	8–15 мм (чаще 10 мм); у ламината 5–10 мм по СП 71	практика (требования производителей); норматив (СП 71, п. 8.10.14)		Протокол СМ-влажности стяжки до укладки; паспорт и партия доски.
		Перепад основания под покрытие	правило 2 м и щуп	не более 2 мм на 2 м	практика		
		Зазоры и перепады между досками; скрип; видимый зазор в замке — брак	щуп, рука, шаг	«ступеньки» нет	практика		
		Влажность помещения при укладке и после	гигрометр	не более 60 %, без сквозняков	норматив (СП 71, п. 8.1.7)		
P-13	Двери и плинтусы Полотна и плинтусы — после чистового пола; скрытые полотна после чистовой отделки стен	Отклонение коробки от вертикали	отвес, уровень	1,5 мм на 1 м, не более 3 мм на коробку	практика (ТР 105-00, пересказ)		Коробки скрытых дверей приняты до штукатурки (этап штукатурки); паспорт на полотна.

Допущения и предложения на листе

Основа листа: размеры сняты с плана заказчика, контрольный обмер не выполнен (К-5); высота потолка 2700 мм принята: на плане заказчика не указана (К-5); подрайон климата не задан — принят не северный (жилые от 2,5 м) (К-4); толщины стен приняты: наружные 250 мм, перегородки 120 мм — не обмерены (К-5); разрешённая мощность 15 кВт принята по типовой квартире, технических условий нет (К-6).

См. лист открытых вопросов (лист 6, записи К-4–К-6).

Изм.	Кол.уч	Лист	№ док.	Подп.	Дата
Разраб.		Кырлан А.С.			14.11.26
Пров.					
ГИП					
Н. контр.					
Утв.					

ГД-2026-006-АИ

Квартира 58 м²

Общая площадь 55,23* м² · * размеры приняты, не замерены (реестр — л. 6, 7, К-5)

Дизайн-проект интерьера

Стадия	Лист	Листов
РП	17	108

Чек-лист приёмки по этапам. Лист 3 из 4

М б/м

Кырлан Александр Сергеевич

Чек-лист приёмки по этапам. Лист 4 из 4

По этапам Р-1…Р-N: что проверить, чем, какой допуск и какой акт подписать до закрытия работы

Приёмка по этапам: контрольные точки, допуски и акты скрытых работ (продолжение)

Этап	Контрольная точка (дальше не пускают без подписи)	Что проверяют	Чем	Допуск	Основание	Подпись	Акт скрытых работ / документ
		Зазор между полотном и коробкой по периметру	щуп	2–4 мм по бокам и верху (единого норматива нет)	практика		
		Открывание и закрывание: без перекоса, плавный ход петель и доводчика	визуально, от руки	без задевания коробки и пола	практика		
Р-14	Чистовая электрика и сантехника Чистовая электрика и сантехника: протокол электролаборатории и проверка УЗО до подписи акта	УЗО: кнопка «Тест»; время отключения; ток отключения	кнопка на аппарате; прибор проверки УЗО (не мультиметр)	отключает; не более 0,3 с; 50–100 % от IΔn	практика измерений		Протокол измерений аккредитованной электролаборатории (изоляция по группам, УЗО, PE, фаза-ноль); исполнительная схема щита; акт опрессовки приложен (этап ВК).
		Сопротивление изоляции готовых линий; петля фаза-ноль для срабатывания автоматов	мегаомметр; прибор петли фаза-ноль	изоляция не менее 0,5 МОм; петля — по проекту	норматив (ПУЭ, гл. 1.8) / по проекту		
		Смесители, сифоны, гибкая подводка: пробный пуск воды	визуально под нагрузкой	нет подтёков в контрольное время	практика		
Р-15	Кухня и мебель Кухня и мебель: замер кухни снят по готовым стенам; чистовая электрика и сантехника подведены	Привязка выводов и розеток к модулям кухни; вытяжка, вентиляция	рулетка, сверка с листом кухни	по проекту кухни	практика		Акт передачи кухни; паспорта техники и гарантийные талоны.
		Тяга вентиляции у решёток	лист бумаги у решётки	бумага притягивается; при сомнениях — замер анемометром	практика		
Р-16	Сдача Финальная приёмка по таблицам СП 71: дефектная ведомость и акт	Стены, потолки, полы, плитка, двери, окна осмотр по чек-листу этапов выше	правило 2 м, уровень, щуп, боковой свет, влагомер	по таблицам выше	практика		Дефектная ведомость и акт приёмки; гарантия: по умолчанию претензии по качеству работ — 2 года, в договоре прописывается отдельно.
		Полный пакет документов: акты скрытых работ, протокол электролаборатории, акт опрессовки, исполнительные схемы, гарантийные обязательства	комплектность	пакет собран до подписи акта	практика		

Примечания

1. Метка основания: «норматив» — цифра подтверждена текстом СП, ГОСТ или ПУЭ; «практика» — отраслевая конвенция или один источник: к спору не годится без сверки первоисточника (СП 71.13330.2017, СП 29.13330, СП 163.1325800.2014, ПУЭ гл. 1.8, СП 73.13330, СП 30.13330).
2. Класс штукатурки (простая / улучшенная / высококачественная) и класс основания под окраску (Q3 или Q4) называются в договоре подряда: допуск выбирается по ним. Q-классы — не норматив, а согласованный сторонами критерий.
3. Акт скрытых работ подписывают до того, как работа закрыта следующим слоем (штукатуркой, плиткой, стяжкой, обшивкой): постфактум он слабее — осматривать нечего. Подписывают заказчик (или технадзор), подрядчик; при перепланировке — автор проекта. Каждую зону снимают до закрытия с рулеткой в кадре и привязкой к стене.
4. По умолчанию, если срок не прописан в договоре, претензии по качеству работ можно предъявить в течение 2 лет со дня приёмки; в договоре гарантийный срок и сроки на скрытые работы рекомендуется назвать явно.

Допущения и предложения на листе

Основа листа: размеры сняты с плана заказчика, контрольный обмер не выполнен (К-5); высота потолка 2700 мм принята: на плане заказчика не указана (К-5); подрайон климата не задан — принят не северный (жилые от 2,5 м) (К-4); толщины стен приняты: наружные 250 мм, перегородки 120 мм — не обмерены (К-5); разрешённая мощность 15 кВт принята по типовой квартире, технических условий нет (К-6).

См. лист открытых вопросов (лист 6, записи К-4–К-6).

Изм.	Кол.уч	Лист	№ док.	Подп.	Дата
Разраб.		Кырлан А.С.			14.11.26
Пров.					
ГИП					
Н. контр.					
Утв.					

ГД-2026-006-АИ

Квартира 58 м²

Общая площадь 55,23* м² · * размеры приняты, не замерены (реестр — л. 6, 7, К-5)

Дизайн-проект интерьера	Стадия	Лист	Листов
	РП	18	108

Чек-лист приёмки по этапам. Лист 4 из 4

М б/м

Кырлан Александр Сергеевич

Лист → мастер

Мастер → листы альбома и документы, которые ему нужны

Какому мастеру какие листы (номера — как в штампе)

Мастер	Что делает по альбому	Листы	Кроме чертежей — документы	Листов
Замерщик и прораб (до начала работ)	Контрольный обмер на голых стенах, сверка размеров и диагоналей, ответы на открытые вопросы до заказа	2–10, 20	Задание на контрольный обмер; лист открытых вопросов	10
Гипсокартонщик и монтажник перегородок	Демонтаж и возведение перегородок, каркас, короба инсталляции, ниши, потолки; закладные под навесное	21, 48–50, 71, 73	Ведомость материалов каркаса; акт скрытых работ на каркас	6
Электрик	Группы щита, подрозетники и высоты, трассы, свет, управление светом, слаботочка, тёплый пол	28–35, 47, 77–93	Таблица нагрузок; ведомость изделий; протокол электролаборатории	26
Сантехник	Выводы воды и канализации, разводка, аксонометрии, инсталляции, короба стояков	38–46, 77–93	Спецификация ВК; акт опрессовки; акт пролива	26
Монтажник вентиляции, отопления и кондиционеров	Вентиляция, радиаторы и тёплые полы, кондиционеры: места, размеры, трассы и дренаж	36–37	Акт опрессовки азотом (кондиционеры); фото воздуховодов до закрытия	2
Штукатур, шпаклёвщик, маляр, паркетчик	Основание стен, окраска и обои по колерной карте, полы и пороги, плинтус, узлы стыков	55–59, 77–94	Колерная карта и выкрасы; спецификация отделочных материалов	23
Плиточник	Раскладка и подрезка плитки стен, пола и фартука, гидроизоляция, швы, выводы в плитке	43–45, 51–54, 77–94	Ведомость плитки; акт теста проливом	25
Монтажник дверей и окон	Заполнение проёмов: размеры коробок, открывание, пороги, скрытые двери	22	Ведомость проёмов; паспорта на полотна	1
Мебельщик, кухонный монтажник	Кухня и мебель на заказ: габариты, членение, фурнитура, связка с электрикой и сантехникой	24–27, 66–75	Ведомость изделий; замер кухни по готовым стенам	14
Заказчик и комплектатор	Что и когда покупать, сколько с запасом, во что это обойдётся; свет, декор и текстиль; визуализации как должно получиться	1, 11–14, 47, 60–61, 64–65, 95–108	Список покупок; смета; календарный график	24
Прораб и технадзор (приёмка)	Приёмка этапов, акты скрытых работ, дефектная ведомость	14–19	Чек-лист приёмки по этапам; календарный график	6

Примечания

1. Номера листов — как в основной надписи: основные подряд (1, 2, 3…), «Д» — детализация мебели, «С» — ведомости, спецификации, узлы и сметы, «П» — приложение единого комплекта. «12–18» — все листы с 12 по 18.
2. Лист может быть у нескольких мастеров: развёртка стены нужна электрику (высоты точек), сантехнику (выводы), отделочнику (материалы) и плиточнику (раскладка). Общие листы (обмер, список листов, перечень вопросов) прораб раздаёт всем.
3. Мастер работает по чертежам и берёт в руки то, что назначено ему здесь; закупки, смету и график ведёт заказчик с прорабом. Лист, которого нет в таблице ни у одного мастера, — вопрос прорабу: чей он.

Допущения и предложения на листе

Основа листа: размеры сняты с плана заказчика, контрольный обмер не выполнен (К-5); высота потолка 2700 мм принята: на плане заказчика не указана (К-5); подрайон климата не задан — принят не северный (жилые от 2,5 м) (К-4); толщины стен приняты: наружные 250 мм, перегородки 120 мм — не обмерены (К-5); разрешённая мощность 15 кВт принята по типовой квартире, технических условий нет (К-6).

См. лист открытых вопросов (лист 6, записи К-4–К-6).

Изм.	Кол.уч	Лист	№ док.	Подп.	Дата
Разраб.		Кырлан А.С.			14.11.26
Пров.					
ГИП					
Н. контр.					
Утв.					

ГД-2026-006-АИ

Квартира 58 м²

Общая площадь 55,23* м² · * размеры приняты, не замерены (реестр — л. 6, 7, К-5)

Дизайн-проект интерьера

Стадия	Лист	Листов
РП	19	108

Лист → мастер

М б/м

Кырлан Александр Сергеевич

01

Архитектурные решения




Кырлан Александр Сергеевич

выпуск 14.11.2026 bcee049e32 · стр. 20 из 128

Обмерный план

Существующее положение · размеры в мм · отметки от чистого пола

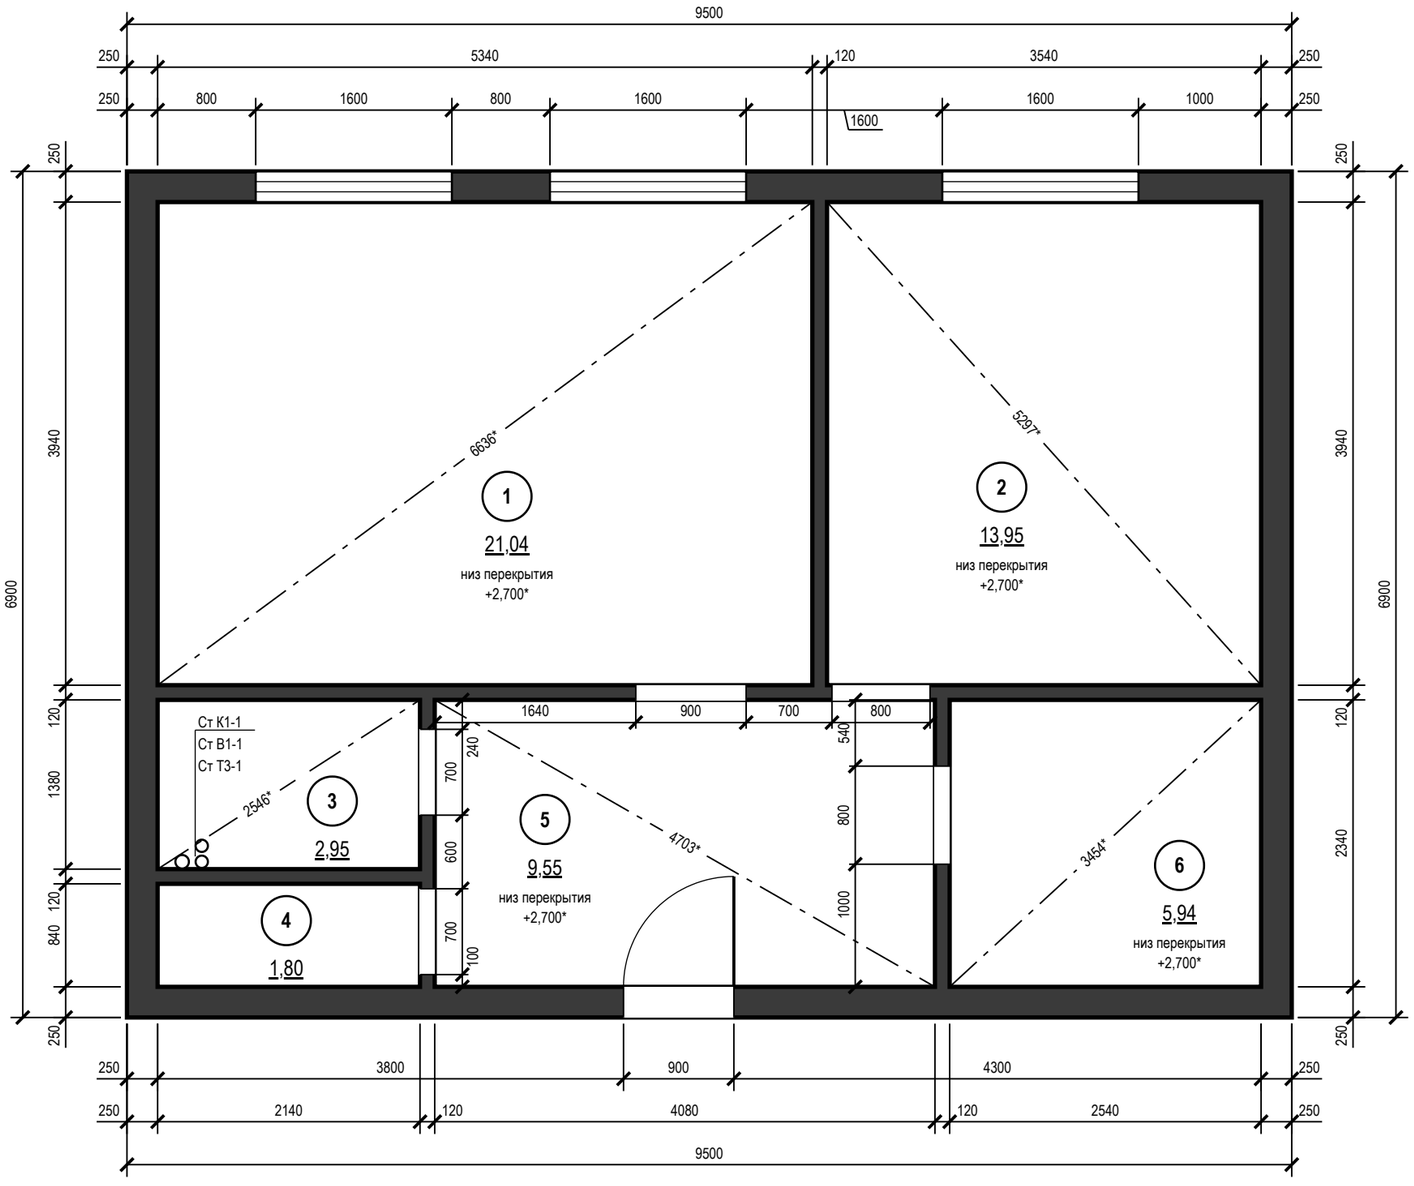

Экспликация помещений

№	Наименование	Площадь, м²
1	Кухня-гостиная	21,04
2	Спальня	13,95
3	Ванная	2,95
4	Санузел	1,80
5	Прихожая	9,55
6	Гардеробная	5,94
	Итого (общая площадь)	**55,23**

Условные обозначения

- существующие стены (сечение)
- окно (рама, остекление)
- проём существующий, без заполнения (откосы)
- стояк: К1 — канализация, В1 — ХВС, Т3 — ГВС
- диагональ помещения — контроль прямоугольности
- (1) номер помещения, площадь м²

Примечания

1. Размеры — в мм по чистым поверхностям стен до отделки (по плану заказчика); площади — в м² по тем же размерам. До начала работ выполнить контрольный обмер.
2. За отметку ±0,000 принят чистый пол, не существующий (блок отметок). «Низ перекрытия» у марки помещения — отметка низа перекрытия от ±0,000, как на развёртках и плане потолков (не высота потолка: потолок — по плану потолков); отметка со знаком «*» — принятая, не замер (вопрос К-5).
3. Толщины стен: наружные 250 мм, перегородки 120 мм; отличающиеся толщины и уступы размерами на плане.
4. Несущие стены не определены: до технического заключения все стены считать несущими; проёмы и штробы в них не выполнять.
5. Дверные проёмы показаны без заполнения (двери — лист 22); высота дверных проёмов 2100 мм; низ окон (подоконник) 800 мм от чистого пола, высота окон 1600 мм.
6. Диагонали — контрольные размеры; «*» — расчёт по принятому контуру (К-5), при обмере заменить замеренным; расхождение более 5 мм подписать на плане как перекос.
7. Размеры проверить на месте до начала работ; расхождение контрольных промеров ≤ 2 %.
8. Размеры короче 1 мм на листе цепочкой не показаны (две выносные линии на таком расстоянии сливаются): пом. 5, стена А — 40 мм от проёма до угла.

Отметки по высоте

±0,000	чистый пол пом. 1, 2, 5, 6; отсчёт высот
−0,015	чистый пол пом. 3, 4, ниже на 15 мм
−0,064*	верх плиты — расчёт, не замер (задание на обмер)
сущ. пол	снимается до плиты; не замерен (задание на обмер)

Допущения и предложения на листе

Основа листа: размеры сняты с плана заказчика, контрольный обмер не выполнен (К-5); высота потолка 2700 мм принята: на плане заказчика не указана (К-5); подрайон климата не задан — принят не северный (жилые от 2,5 м) (К-4); толщины стен приняты: наружные 250 мм, перегородки 120 мм — не обмерены (К-5); разрешённая мощность 15 кВт принята по типовой квартире, технических условий нет (К-6).

Открытые вопросы и конфликты по листу: К-5.

См. лист открытых вопросов (лист 6, записи К-4–К-6).

1000 мм · печать 1:1

Изм.	Кол.уч	Лист	№ док.	Подп.	Дата
Разраб.		Кырлан А.С.			14.11.26
Пров.					
ГИП					
Н. контр.					
Утв.					

ГД-2026-006-АИ

Квартира 58 м²

Общая площадь 55,23* м² · * размеры приняты, не замерены (реестр — л. 6, 7, К-5)

Дизайн-проект интерьера

Стадия	Лист	Листов
РП	20	108

Обмерный план


М 1:50

Кырлан Александр Сергеевич

План демонтажа и монтажа перегородок

Перепланировка не выполняется · существующие стены сохраняются · размеры в мм


ПРЕДВАРИТЕЛЬНО · не для производства работ · открыто пунктов: 9 (реестр — л. 6, 7)

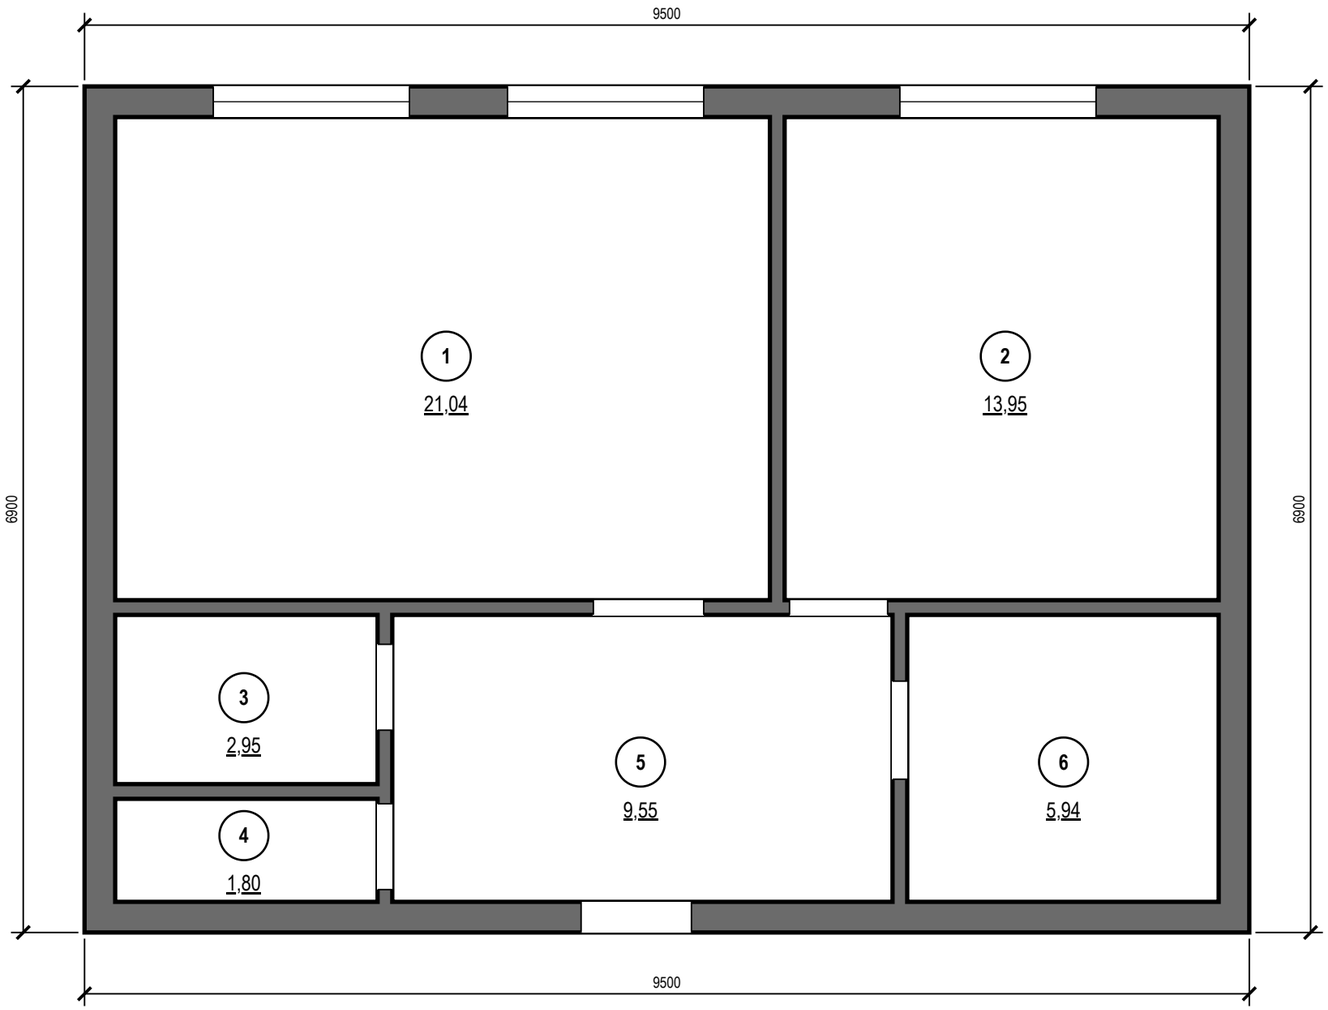

Условные обозначения

- существующие стены — сохраняются;
- несущие не определены — считать несущими
- демонтируемые конструкции — на плане нет
- возводимые перегородки — на плане нет
- проём существующий, без заполнения (откосы)
- (1) номер помещения, площадь м²

Отметки по высоте

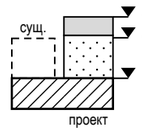

±0,000	чистый пол пом. 1, 2, 5, 6; отсчёт высот
−0,015	чистый пол пом. 3, 4, ниже на 15 мм
−0,064*	верх плиты — расчёт, не замер (задание на обмер)
сущ. пол	снимается до плиты; не замерен (задание на обмер)

Примечания

1. Перепланировка не выполняется: несущие и ненесущие стены, перегородки и плиты перекрытия не демонтируются, новые стены не возводятся; существующие стены и перегородки сохраняются.
2. Дверные блоки — по плану дверей (лист 22); существующие проёмы не расширяются.
3. Демонтаж существующих покрытий пола, стен и потолка, дверных блоков и сантехприборов (если есть) — до основания; объёмы демонтажа — для справки, по факту на объекте.
4. За отметку ±0,000 принят чистый пол, не существующий (блок отметок). Размеры — в мм по чистовой поверхности стен до отделки.
5. Размеры проверить на месте до начала работ: расхождение с обмером — не более 2 % (иначе — к архитектору).
6. Несущие стены не определены: до технического заключения все стены считать несущими — проёмы, ниши и штробы в них не выполнять.

Допущения и предложения на листе

Основа листа: размеры сняты с плана заказчика, контрольный обмер не выполнен (К-5); высота потолка 2700 мм принята: на плане заказчика не указана (К-5); подрайон климата не задан — принят не северный (жилые от 2,5 м) (К-4); толщины стен приняты: наружные 250 мм, перегородки 120 мм — не обмерены (К-5); разрешённая мощность 15 кВт принята по типовой квартире, технических условий нет (К-6).

См. лист открытых вопросов (лист 6, записи К-4–К-6).

1000 мм · печать 1:1

Изм.	Кол.уч	Лист	№ док.	Подп.	Дата
Разраб.		Кырлан А.С.			14.11.26
Пров.					
ГИП					
Н. контр.					
Утв.					

ГД-2026-006-АИ

Квартира 58 м²

Общая площадь 55,23* м² · * размеры приняты, не замерены (реестр — л. 6, 7, К-5)

Дизайн-проект интерьера

Стадия	Лист	Листов
РП	21	108

План демонтажа и монтажа перегородок

М 1:50

Кырлан Александр Сергеевич

выпуск 14.11.2026 № bcee049e32 · стр. 22 из 128

План дверей и ведомость заполнения проёмов


Проёмы, марки заполнения, привязки · размеры в мм

Условные обозначения

- стены (подложка обмера)
- дверь распашная, дуга открывания
- дверь скрытого монтажа
- дверь входная (полотно толще)
- оконный блок
- Д — марка типа (Д-N, ОК-N)
- 1 — номер помещения, площадь м²

Примечания

1. Размеры проёмов и привязки — в миллиметрах от чистых граней стен до отделки; привязка — от угла того помещения, со стороны которого стоит размер. Размер проёма — ширина × высота от чистого пола 0,000. Размеры на плане — проёмов, не полотен: полотно — в ведомости, коробка — по системе. Откос от угла помещения до проёма с коробкой — не менее 50 мм.
2. Марки в кружках — типы заполнения проёмов (ГОСТ 21.501-2018, п. 5.3.2); одна марка — один типоразмер; количество сверено с планом.
3. Открывание: Л — петли слева, П — справа, если смотреть со стороны, куда открывается полотно (на себя).
4. Скрытые двери (Д-2…Д-4): проём замерить в чистоте; блок заказать до штукатурки (≈ 30 дн.), короб ставить до штукатурки; полотно навесить после чистовой отделки, красить в цвет стен. Порядок практика монтажа, изготовитель подтверждает.
5. Д-2…Д-4 — существующие проёмы, до техзаключения не расширять (К-3).
6. Полотно «расч.» — по проёму с запасом по каталогам, заказ — по таблице проёмов модели; Д-2…Д-4: проём 2100, а под полотно 2000 по каталогам нужен 2050–2080, под 2100 — 2150–2180: высоту проёма по модели; Д-1: входной блок по ГОСТ 31173-2016 — задать при выборе блока.
7. Экспликация помещений — лист 20; в марках помещений — номер и площадь, м².
8. Привязка проёма к углу помещения меньше 1 мм на листе, размер на плане не показан: Д-3 — 40 мм; Д-4 — 40 мм.

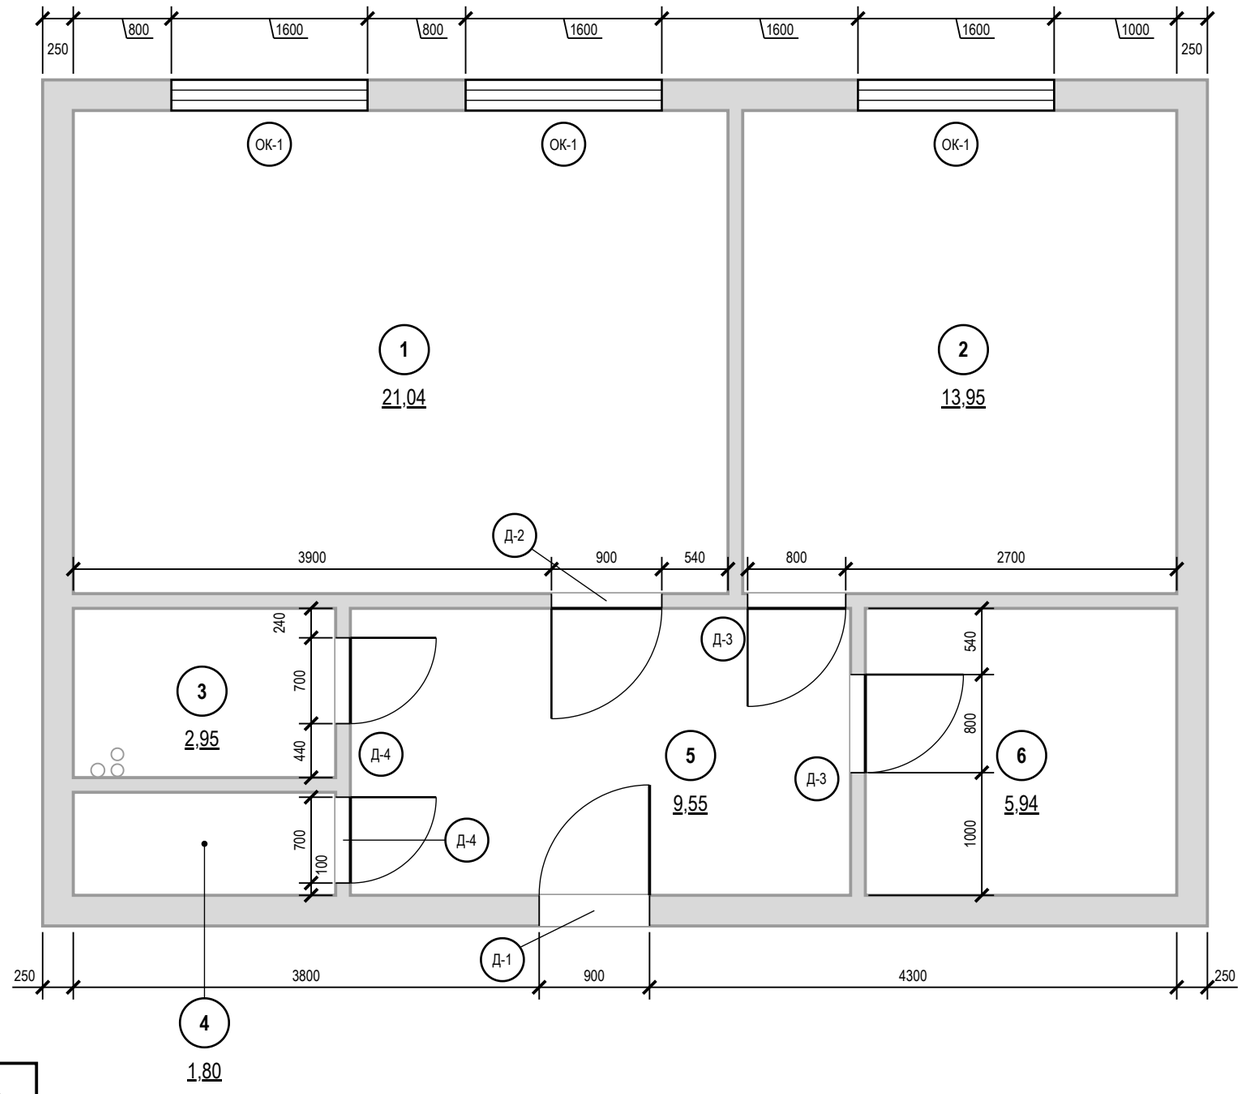

Ведомость заполнения проёмов

Марка	Наименование, обозначение	Проём ш×в, мм	Полотно (расч.)	Кол.	Откр.	Отделка полотна	Фурнитура	Прим.
Д-1	Блок дверной входной, ГОСТ 31173-2016	900×2100	блок задать	1	Л	в комплекте блока	в комплекте блока (замки, глазок)	
Д-2	Дверь скрытого монтажа, Софья (SOFIA) Скрытые двери	900×2100	800×2000	1	Л	S 1502-Y50R — пом. 5, S 1002-Y50R — пом. 1	скрытые петли 3D, магнитный замок	
Д-3	Дверь скрытого монтажа, Софья (SOFIA) Скрытые двери	800×2100	700×2000	2	Л, П	окраска S 1502-Y50R с двух сторон; V503 пом. 6, S 1502-Y50R пом. 5	скрытые петли 3D, магнитный замок	
Д-4	Дверь скрытого монтажа, Софья (SOFIA) Скрытые двери	700×2100	600×2000	2	П, П	S 1502-Y50R — пом. 5, в тон облицовки — пом. 3; S 1502-Y50R — пом. 5, в тон облицовки пом. 4	скрытые петли 3D, магнитный замок, фиксатор WC	порог 15
ОК-1	Блок оконный, ГОСТ 23166-2021	1600×1600		3				низ 800

Допущения и предложения на листе

Основа листа: размеры сняты с плана заказчика, контрольный обмер не выполнен (К-5); высота потолка 2700 мм принята: на плане заказчика не указана (К-5); подрайон климата не задан — принят не северный (жилые от 2,5 м) (К-4); толщины стен приняты: наружные 250 мм, перегородки 120 мм — не обмерены (К-5); разрешённая мощность 15 кВт принята по типовой квартире, технических условий нет (К-6).

Открытые вопросы и конфликты по листу: К-3.

См. лист открытых вопросов (лист 6, записи К-3–К-6).

1000 мм · печать 1:1

Изм.	Кол.уч	Лист	№ док.	Подп.	Дата
Разраб.		Кырлан А.С.			14.11.26
Пров.					
ГИП					
Н. контр.					
Утв.					

ГД-2026-006-АИ

Квартира 58 м²

Общая площадь 55,23* м² · * размеры приняты, не замерены (реестр — л. 6, 7, К-5)

Дизайн-проект интерьера

Стадия	Лист	Листов
РП	22	108

План дверей и ведомость заполнения проёмов

М 1:50

Кырлан Александр Сергеевич

выпуск 14.11.2026 № bcee049e32 · стр. 23 из 128

02

Планировочное решение

Кырлан Александр Сергеевич

выпуск 14.11.2026 bcee049e32 · стр. 24 из 128


Концепция интерьера

Скандинавский · схема нейтральная · 60/30/10 · материалы, образы и зонирование

Идея

Стиль — скандинавский: светло, спокойно, уютно (hygge), естественно, функционально, в меру (lagom). Палитра выведена из выкрасов (колерная карта): база — тёплые нейтрали NCS S 1502-Y50R / S 1002-Y50R на стенах, NCS S 0300-N на потолках; второй цвет — Tikkurila V503 (гардеробная); акцент — пыльный синий NCS S 4010-R90B в текстиле по концепции стиля (ИЗ-4). Цветовая схема — нейтральная, пропорция 60/30/10: база на стенах и потолках, вторичный цвет — в текстиле и мягкой мебели, акцент — точечно.

Мудборд: материалы и фактуры

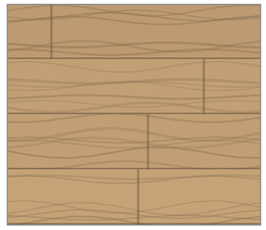

Инженерная доска, дуб натуральный
пол



SG651622R
пол



NCS S 0300-N
потолок, плинтус




NCS S 1502-Y50R
стены




NCS S 1002-Y50R
стены



Winter · Tikkurila V503
стены, потолок, плинтус

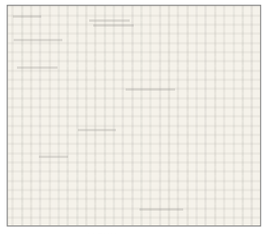

Лён, Tikkurila G503
шторы льняные в пол, римская штора льняная с блэкаут-подкладкой

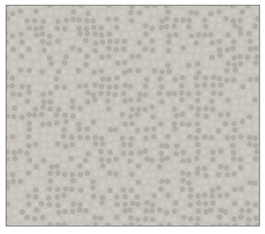

Шерсть, NCS S 2002-Y
ковёр шерстяной плоского плетения 1400×2500



Букле, Tikkurila G503
подушки на диван

Палитра 60/30/10

	60 %		30 %	10 %

60 % база — NCS S 1502-Y50R, LRV 72; NCS S 1002-Y50R, LRV 82; NCS S 0300-N, LRV 92

30 % вторичный — Tikkurila V503 Winter, LRV 86

10 % акцент — NCS S 4010-R90B, LRV 27

Функциональное зонирование (М 1:100)



- дневная зона: гостиная, кухня, столовая
- ночная зона: спальни
- мокрая зона: санузлы
- хранение: гардеробная, кладовая
- вход и коммуникации
- функциональная зона в помещении
- (1) номер помещения (лист 24)

Образы помещений

1. Кухня-гостиная 21,04 м²

стены NCS S 1002-Y50R
пол — доска, дуб натуральный
текстиль: шторы льняные в пол G503, шторы льняные в пол G503, ковёр шерстяной плоского плетения 1400×2500 S 2002-Y
декор: постер над диваном, постер над диваном,

2. Спальня 13,95 м²

стены NCS S 1502-Y50R
пол — доска, дуб натуральный
текстиль: римская штора льняная с блэкаут-подкладкой G503, ковёр шерстяной 2000×3000 No. 241
декор: картина над кроватью, зеркало в рост,

5. Прихожая 9,55 м²

стены NCS S 1502-Y50R
пол — SG651622R
декор: зеркало в рост, постер между дверями
свет 3000 K

6. Гардеробная 5,94 м²

стены Tikkurila V503
пол — доска, дуб натуральный
свет 3000 K

3. Ванная 2,95 м²

стены Italon 610015000370
пол — SG651622R
текстиль: полотенца банные махровые S 4010-R90B, полотенца для рук вафельные G503, коврик для ванной у бортика ванны S 4010-R90B
декор: зеркало над умывальником

4. Санузел 1,80 м²

стены Italon 610015000370
пол — SG651622R
декор: постер в тонкой, ваза-бутыль керамическая, свеча в янтарном
свет 3000 K

Материалы и отделка

Инженерная доска, дуб натуральный
масло, 1-полосная, 14/4 мм
пол — пом. 1, 2, 6

SG651622R
пол — пом. 3, 4, 5

610015000370
стены — пом. 3, 4

NCS S 1002-Y50R, LRV 82
стены — пом. 1

NCS S 0300-N, LRV 92
глубокоматовая
потолок, плинтус — пом. 1, 2, 3, 4, 5

NCS S 1502-Y50R, LRV 72
глубокоматовая
стены — пом. 2, 5

Tikkurila V503 Winter, LRV 86
Tikkurila Harmony, матовая
стены, потолок, плинтус — пом. 6

Текстиль и металл

Лён, Tikkurila G503
шторы льняные в пол, римская штора льняная с блэкаут-подкладкой

Букле, Tikkurila G503
подушки на диван

Шерсть, NCS S 3010-G10Y
плед шерстяной на диван

Лён, NCS S 3010-G10Y
подушки декоративные на кровать

Шерсть, NCS S 4010-R90B
плед шерстяной крупной вязки в изножье кровати, коврик для ванной у бортика ванны

Шерсть, NCS S 2002-Y
ковёр шерстяной плоского плетения 1400×2500

Лён, NCS S 4010-R90B
подушки на диван, полотенца банные махровые

Шерсть, Farrow & Ball No. 241
ковёр шерстяной 2000×3000 под кроватью

Букле, NCS S 4010-R90B
подушка-валик на кровать

Чёрный матовый металл
постер в тонкой

Чего избегаем

1) Холодный белый + серый ламинат + серый диван без дерева
2) Принты олени/Hygge, надписи, лишние подушки
3) Глянцевый лак на дереве, венге, под орех
4) Одна люстра на комнату, свет 4000–6500 K, споты сеткой
5) Тяжёлые шторы с ламбрекенами, лепнина, многоуровневые потолки
6) Три разных светлых дуба в одном помещении

Допущения и предложения на листе

Основа листа: размеры сняты с плана заказчика, контрольный обмер не выполнен (К-5); высота потолка 2700 мм принята: на плане заказчика не указана (К-5); подрайон климата не задан — принят не северный (жилые от 2,5 м) (К-4); толщины стен приняты: наружные 250 мм, перегородки 120 мм — не обмерены (К-5); разрешённая мощность 15 кВт принята по типовой квартире, технических условий нет (К-6).
См. лист открытых вопросов (лист 6, записи К-4–К-6).

Примечания

1. Коды цвета — по веерам производителей (колерная карта, лист 57); перед закупкой краски — выкрас на стене объекта под дневным светом и лампами проекта.
2. Материалы — по ведомости отделки (лист 56); мебель, текстиль и декор — по спецификации (лист 25). Образцы доски, керамогранита и тканей утвердить до заказа.
3. Фактуры на листе условные, цвет передан по HEX-значениям производителей: при печати возможны отклонения, решение — только по физическому образцу.

Изм.	Кол.уч	Лист	№ док.	Подп.	Дата
Разраб.		Кырлан А.С.			14.11.26
Пров.					
ГИП					
Н. контр.					
Утв.					

ГД-2026-006-АИ

Квартира 58 м²

Общая площадь 55,23* м² · * размеры приняты, не замерены (реестр — л. 6, 7, К-5)

Дизайн-проект интерьера

Стадия	Лист	Листов
РП	23	108


Концепция интерьера
М б/м

Кырлан Александр Сергеевич

выпуск 14.11.2026 № bcee049e32 · стр. 25 из 128

План расстановки мебели

Мебель и оборудование · размеры в мм от чистовых стен · марки — по ведомости

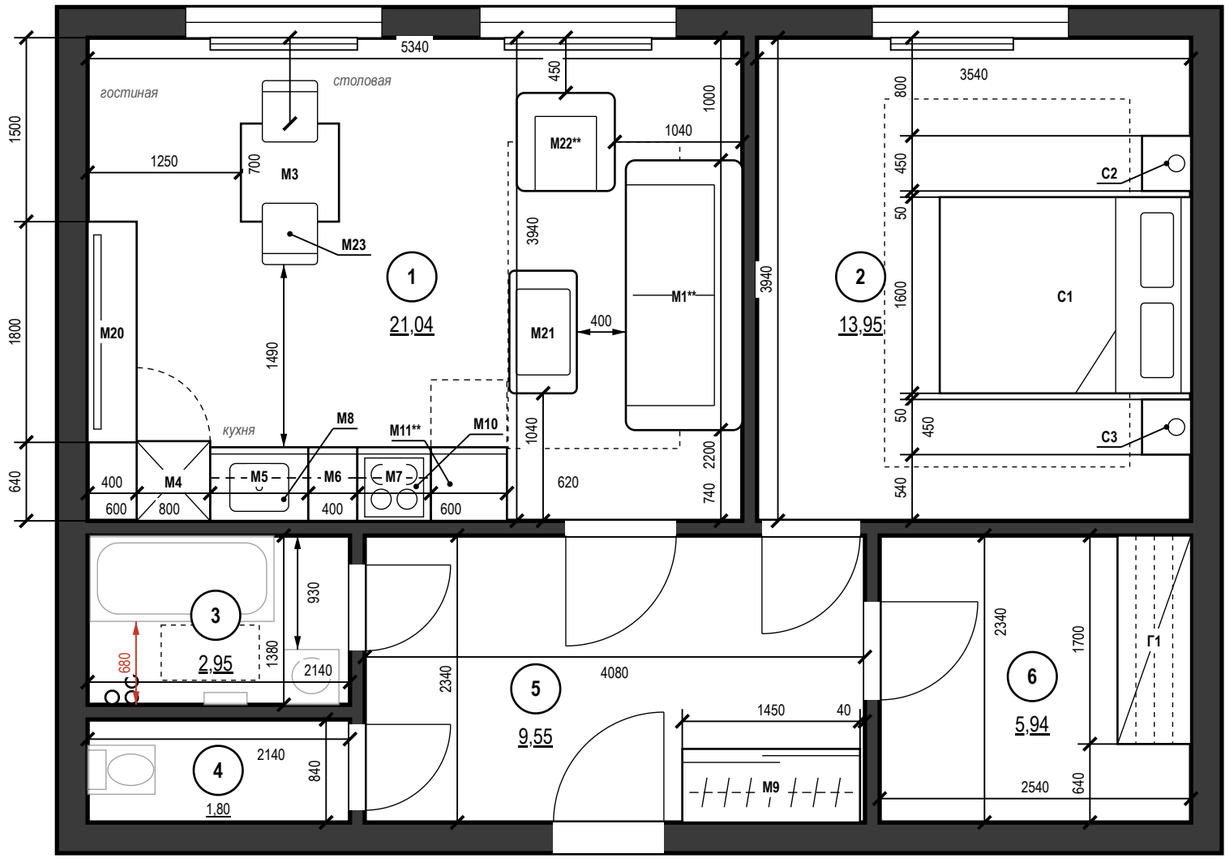

Экспликация помещений

лист 20 · на плане — номера в марках

Ведомость мебели и оборудования

Марка	Наименование	Ш×Г×В, мм	Пом.	Кол.
М4	Пенал кухонный	600×650×2100	1	1
М5	Модуль нижний	800×600×900	1	1
М6	Модуль нижний	400×600×900	1	1
М7	Модуль нижний	600×600×900	1	1
М11**	Ниша под стиральную машину	620×600×900	1	1
М8	Модуль навесной	1200×350×720	1	1
М10	Навесной модуль над варочной	600×350×620	1	1
М1**	Диван	2200×950×850	1	1
М3	Стол обеденный	800×800×750	1	1
М20	ТВ-тумба подвесная с экраном	1800×400×450	1	1
М21	Стол журнальный	550×1000×400	1	1
М22**	Кресло	800×800×800	1	1
С1	Кровать двуспальная	1600×2050×450	2	1
С2	Тумба прикроватная	450×400×500	2	1
С3	Тумба прикроватная	450×400×500	2	1
М9	Шкаф-купе	1450×600×2450	5	1
Г1	Система хранения	1700×600×2400	6	1
М23	Стул обеденный к столу М3	450×500×820	1	2

Ш — вдоль стены (изголовья), Г — от стены (длина кровати)

Материалы, модели, допуск замены — лист 25

Условные обозначения

- мебель и оборудование — габарит в масштабе
- навесные шкафы (низ выше 0,9 м) — невидимый контур
- ковёр
- зона открывания дверец шкафов и техники
- **К1** — марка предмета по ведомости мебели
- привязка от чистовой стены, мм
- ширина прохода, зазор, мм
- проход меньше нормы — расстановку изменить
- сантехприборы — подложка (лист ВК)
- радиатор отопления (лист ОВ)
- существующие стены (сечение)
- стояк: К1 — канализация, В1 — ХВС, Т3 — ГВС
- (1) — номер помещения, площадь м²
- *зона* — функциональная зона помещения

Примечания

1. Размеры — в мм от чистовых поверхностей стен, размеры помещений — в свету, привязки — от стен, углов помещения и соседних предметов, проходы и зазоры — стрелками; розетки и выводы под мебель — лист 28, выключатели — лист 30, сантехприборы — лист 38.
2. Общие указания к расстановке (чистовой слой, контрольный обмер, зазоры встроенной мебели, замена покупной) — примечания к спецификации, лист 25.
3. Стулья обеденной группы (М23 — 2 шт.) показаны в рабочем положении, задвинутыми под столешницу на 150 мм.

Допущения и предложения на листе

Основа листа: размеры сняты с плана заказчика, контрольный обмер не выполнен (К-5); высота потолка 2700 мм принята: на плане заказчика не указана (К-5); подрайон климата не задан — принят не северный (жилые от 2,5 м) (К-4); толщины стен приняты: наружные 250 мм, перегородки 120 мм — не обмерены (К-5); разрешённая мощность 15 кВт принята по типовой квартире, технических условий нет (К-6).

Знак «**» — предложение проектировщика, заказчиком не утверждено (согласовать с заказчиком): ИЗ-2: М22 — Было x 4250 — место занял диван М1 (x 4450…5400 от y 1000); ИЗ-2, ИЗ-4: М1 — Было offset 1300…3500: торец дивана в 500 мм от стены В, правые 350 мм проёма Д-2 (3900…4800) упирались в диван; К-7: М11 — место стиральной машины: вместо модуля с ящиками 400 справа от варочной; ряд до 3420, журнальный стол М21 (с x 3440) не мешает загрузке.

Открытые вопросы и конфликты по листу: К-2, К-7.

См. лист открытых вопросов (лист 6, записи К-2, К-4–К-7; лист 7, записи ИЗ-2, ИЗ-4).

1000 мм · печать 1:1

Изм.	Кол.уч	Лист	№ док.	Подп.	Дата
Разраб.		Кырлан А.С.			14.11.26
Пров.					
ГИП					
Н. контр.					
Утв.					

ГД-2026-006-АИ

Квартира 58 м²

Общая площадь 55,23* м² · * размеры приняты, не замерены (реестр — л. 6, 7, К-5)

Дизайн-проект интерьера

Стадия	Лист	Листов
РП	24	108

План расстановки мебели

М 1:50

Кырлан Александр Сергеевич

выпуск 14.11.2026 № bcee049e32 · стр. 26 из 128

Спецификация мебели и оборудования

ПРЕДВАРИТЕЛЬНО · не для производства работ · открыто пунктов: 9 (реестр — л. 6, 7)

Форма 1 ГОСТ 21.110-2013 · позиции мебели — по плану расстановки

Поз.	Наименование и техническая характеристика	Тип, марка, обозначение документа, опросного листа	Код продукции	Поставщик	Ед. измерения	Кол.	Масса 1 ед., кг	Примечание
	Мебель встроенная и корпусная (изготовление по чертежам мебельщика)							
М4	Пенал кухонный, холодильник; корпус ЛДСП 16 мм; фасады — без фасада (прибор отдельностоящий); Ш×Г×В 600×650×2100 мм	—	—	изготовление на заказ	шт.	1	—	пом. 1
М5	Модуль нижний, мойка; корпус ЛДСП 16 мм; фасады — МДФ эмаль 18 мм; Ш×Г×В 800×600×900 мм	—	—	изготовление на заказ	шт.	1	—	пом. 1
М6	Модуль нижний; корпус ЛДСП 16 мм; фасады — МДФ эмаль 18 мм; Ш×Г×В 400×600×900 мм	—	—	изготовление на заказ	шт.	1	—	пом. 1
М7	Модуль нижний, варочная; корпус ЛДСП 16 мм; фасады — МДФ эмаль 18 мм; Ш×Г×В 600×600×900 мм	—	—	изготовление на заказ	шт.	1	—	пом. 1
М8	Модуль навесной; корпус ЛДСП 16 мм; фасады — МДФ эмаль 18 мм; Ш×Г×В 1200×350×720 мм	—	—	изготовление на заказ	шт.	1	—	пом. 1
М10	Навесной модуль над варочной, вытяжка встраивается в дно; корпус ЛДСП 16 мм; фасады — МДФ эмаль 18 мм; Ш×Г×В 600×350×620 мм	—	—	изготовление на заказ	шт.	1	—	пом. 1
М11**	Модуль под встраиваемую ПММ 60; без корпуса (ниша между соседними модулями); фасад на дверь машины — МДФ эмаль 18 мм; цоколь; Ш×Г×В 620×600×900 мм	—	—	изготовление на заказ	шт.	1	—	пом. 1
М9	Шкаф-купе; корпус ЛДСП 16 мм; фасады — ЛДСП 10 мм в алюминиевом профиле; Ш×Г×В 1450×600×2450 мм	—	—	изготовление на заказ	шт.	1	—	пом. 5
Г1	Система хранения: штанги, полки, ящики; каркас и полки — ЛДСП 16 мм, декор «дуб натуральный»; без фасадов; Ш×Г×В 1700×600×2400 мм	—	—	изготовление на заказ	шт.	1	—	пом. 6; крепление к стене
	Мебель покупная							
М1**	Диван; обивка — ткань, цвет Tikkurila V503; Ш×Г×В 2200×950×850 мм	аналог: Ш×Г×В 2200×950×850 мм, обивка — ткань	—	аналог по характеристикам	шт.	1	—	пом. 1; замена ≤ габарита
М3	Стол обеденный; шпон, дуб натуральный, матовое масло; Ш×Г×В 800×800×750 мм	аналог: Ш×Г×В 800×800×750 мм, шпон	—	аналог по характеристикам	шт.	1	—	пом. 1; замена ≤ габарита
М20	ТВ-тумба подвесная с экраном; шпон, дуб натуральный, матовое масло; Ш×Г×В 1800×400×450 мм	аналог: Ш×Г×В 1800×400×450 мм, шпон	—	аналог по характеристикам	шт.	1	—	пом. 1; замена ≤ габарита
М21	Стол журнальный; шпон, дуб натуральный, матовое масло; Ш×Г×В 550×1000×400 мм	аналог: Ш×Г×В 550×1000×400 мм, шпон	—	аналог по характеристикам	шт.	1	—	пом. 1; замена ≤ габарита
М22**	Кресло; обивка — ткань, цвет Tikkurila V503; Ш×Г×В 800×800×800 мм	аналог: Ш×Г×В 800×800×800 мм, обивка — ткань	—	аналог по характеристикам	шт.	1	—	пом. 1; замена ≤ габарита
М23	Стул обеденный к столу М3; обивка — ткань, цвет Tikkurila V503; каркас — дуб натуральный; Ш×Г×В 450×500×820 мм	аналог: Ш×Г×В 450×500×820 мм, обивка — ткань	—	аналог по характеристикам	шт.	2	—	пом. 1; замена ≤ габарита
С1	Кровать двуспальная; мягкое изголовье, обивка — ткань, цвет Tikkurila V503; Ш×Г×В 1600×2050×450 мм	аналог: Ш×Г×В 1600×2050×450 мм, мягкое изголовье	—	аналог по характеристикам	шт.	1	—	пом. 2; замена ≤ габарита
С2, С3	Тумба прикроватная; шпон, дуб натуральный, матовое масло; Ш×Г×В 450×400×500 мм	аналог: Ш×Г×В 450×400×500 мм, шпон	—	аналог по характеристикам	шт.	2	—	пом. 2; замена ≤ габарита
	Техника встраиваемая и бытовая (покупные изделия), светильники под розетки							
	Холодильник, в модуле М4	аналог по характеристикам: отдельностоящий, габарит — по проёму	—	по выбору заказчика до изготовления мебели	шт.	1	—	пом. 1; по схеме изготовителя
	Стиральная машина, в модуле М11**	аналог по характеристикам: тип загрузки — по листу ВК, по листу ВК	—	по выбору заказчика до изготовления мебели	шт.	1	—	пом. 1; по схеме изготовителя
	Варочная панель встраиваемая, индукционная, в модуле М7	аналог по характеристикам: индукционная 60 см, вырез 560 × 490 мм по шаблону модели	—	по выбору заказчика до изготовления мебели	шт.	1	—	пом. 1; по схеме изготовителя

Примечания

1. Позиции мебели совпадают с марками на плане расстановки (лист 24); размеры Ш×Г×В — Ш вдоль стены, Г от стены.
2. Размеры и привязки плана расстановки — в мм от чистовых поверхностей стен: слой штукатурки 20 мм по блоку и 5 мм шпаклёвки по ГКЛ учтён; привязки — от стен и углов помещения, а не от другой мебели.
3. План расстановки не является документацией для изготовления мебели. Встроенная и корпусная мебель изготавливается по чертежам мебельщика после контрольного обмера (после штукатурки); «стена в стену» — с зазором 10 мм с каждой стороны или с компенсаторами; графы «Тип, марка» и «Код продукции» для неё не заполняются (ГОСТ 21.110-2013).
4. Покупные изделия — аналог по характеристикам: заменять только на изделия не больше указанного габарита и того же материала и цвета.
5. Материал и цвет, не указанные в данных изделия, приняты по концепции (лист 23): тон дерева — по полу, обивка — по вторичному цвету палитры; образцы согласовать до заказа.
6. Масса 1 ед. для изделий до 25 кг не указывается. Техника — по монтажным схемам изготовителя; выводы — по листам ЭОМ и ВК.

Допущения и предложения на листе

Основа листа: размеры сняты с плана заказчика, контрольный обмер не выполнен (К-5); высота потолка 2700 мм принята: на плане заказчика не указана (К-5); подрайон климата не задан — принят не северный (жилые от 2,5 м) (К-4); толщины стен приняты: наружные 250 мм, перегородки 120 мм — не обмерены (К-5); разрешённая мощность 15 кВт принята по типовой квартире, технических условий нет (К-6).

Знак «**» — предложение проектировщика, заказчиком не утверждено (согласовать с заказчиком): ИЗ-2: М22 — Было х 4250 — место занял диван М1 (х 4450…5400 от у 1000); ИЗ-2, ИЗ-4: М1 — Было offset 1300…3500: торец дивана в 500 мм от стены В, правые 350 мм проёма Д-2 (3900…4800) упирались в диван; К-7: М11 — место стиральной машины: вместо модуля с ящиками 400 справа от варочной; ряд до 3420, журнальный стол М21 (с х 3440) не мешает загрузке.

См. лист открытых вопросов (лист 6, записи К-4–К-7; лист 7, записи ИЗ-2, ИЗ-4).

Изм.	Кол.уч	Лист	№ док.	Подп.	Дата
Разраб.		Кырлан А.С.			14.11.26
Пров.					
ГИП					
Н. контр.					
Утв.					

ГД-2026-006-АИ

Квартира 58 м²

Общая площадь 55,23* м² · * размеры приняты, не замерены (реестр — л. 6, 7, К-5)

Дизайн-проект интерьера

Стадия	Лист	Листов
РП	25	108

Спецификация мебели и оборудования

М 6/м

Кырлан Александр Сергеевич

Спецификация мебели и оборудования (продолжение)

Форма 1 ГОСТ 21.110-2013 · позиции мебели — по плану расстановки

Поз.	Наименование и техническая характеристика	Тип, марка, обозначение документа, опросного листа	Код продукции	Поставщик	Ед. измерения	Кол.	Масса 1 ед., кг	Примечание
	Вытяжка встраиваемая, в модуле М10	аналог по характеристикам: производительность — по расчёту ОВ, шум ≤ 55 дБ(А)	—	по выбору заказчика до изготовления мебели	шт.	1	—	пом. 1; по схеме изготовителя
	Кондиционер настенный (сплит-система), внутренний блок, КВ-1**, стена Г, низ — (высота блока не задана, уточнить по паспорту модели) — предложено	аналог по характеристикам: настенный инверторный, 2,5 кВт, блок 900×—×250 мм, дренаж наружу, трасса фреона — по паспорту модели	—	по выбору заказчика до изготовления мебели	шт.	1	—	пом. 1; предложено, решает заказчик; по паспорту модели
	Кондиционер, наружный блок, КН-1, стена А — предложено	аналог по характеристикам: в корзине на фасаде, вынос ≤ 350 мм, доступ для обслуживания с лоджии/окна/автовышки; согласие собственников	—	по выбору заказчика до изготовления мебели	шт.	1	—	пом. 1; предложено, решает заказчик; по паспорту модели
	Кондиционер настенный (сплит-система), внутренний блок, КВ-2*, стена А, низ — (высота блока не задана, уточнить по паспорту модели)	аналог по характеристикам: настенный инверторный, 2 кВт, блок 780×—×220 мм, дренаж наружу, трасса фреона — по паспорту модели	—	по выбору заказчика до изготовления мебели	шт.	1	—	пом. 2; по паспорту модели
	Кондиционер, наружный блок, КН-2, стена А	аналог по характеристикам: в корзине на фасаде, вынос ≤ 350 мм, доступ для обслуживания с лоджии/окна/автовышки; согласие собственников	—	по выбору заказчика до изготовления мебели	шт.	1	—	пом. 2; по паспорту модели
	Торшер, у поз. М3; абажур — ткань или опаловое стекло; лампа 3000 K	—	—	аналог по характеристикам	шт.	1	—	пом. 1; розетка — по плану розеток (ЭОМ)
	Текстиль							
Т1**	Портьеры — шторы льняные в пол, молочные (окно 1); лён 100 %; цвет Tikkurila G503; карниз 2100 мм, высота 2590 мм, сборка 2	—	—	аналог по характеристикам	шт.	2	—	пом. 1
Т2**	Портьеры — шторы льняные в пол, молочные (окно 2); лён 100 %; цвет Tikkurila G503; карниз 2100 мм, высота 2590 мм, сборка 2	—	—	аналог по характеристикам	шт.	2	—	пом. 1
Т3**	Ковёр шерстяной плоского плетения 1400×2500, овсяный; шерсть 100 %; цвет NCS S 2002-Y; 1400×2500 мм	—	—	аналог по характеристикам	шт.	1	—	пом. 1; с подложкой
Т4**	Подушки на диван, букле молочное; букле (шерсть 60 %, полиэстер 40 %); цвет Tikkurila G503	—	—	аналог по характеристикам	шт.	3	—	пом. 1
Т5**	Подушки на диван, лён, пыльный синий; лён 100 %; цвет NCS S 4010-R90B	—	—	аналог по характеристикам	шт.	2	—	пом. 1
Т6**	Плед шерстяной на диван, шалфей; шерсть мериноса 100 %; цвет NCS S 3010-G10Y	—	—	аналог по характеристикам	шт.	1	—	пом. 1
Т7**	Римская штора льняная с блэкаут-подкладкой, молочная; лён 100 %; цвет Tikkurila G503; карниз 1650 мм, высота 1750 мм	—	—	аналог по характеристикам	шт.	1	—	пом. 2
Т8**	Ковёр шерстяной 2000×3000 под кроватью, светлый каменный; шерсть 100 %; цвет Farrow & Ball No. 241; 2000×3000 мм	—	—	аналог по характеристикам	шт.	1	—	пом. 2; с подложкой
Т9**	Подушки декоративные на кровать, лён, шалфей; лён 100 %; цвет NCS S 3010-G10Y	—	—	аналог по характеристикам	шт.	2	—	пом. 2
Т10**	Подушка-валик на кровать, букле, пыльный синий; букле (шерсть 60 %, полиэстер 40 %); цвет NCS S 4010-R90B	—	—	аналог по характеристикам	шт.	1	—	пом. 2
Т11**	Плед шерстяной крупной вязки в изножье кровати, пыльный синий; шерсть мериноса 100 %; цвет NCS S 4010-R90B	—	—	аналог по характеристикам	шт.	1	—	пом. 2
Т12**	Полотенца банные махровые, пыльный синий, сложены на полотенцесушителе; хлопок 100 %; цвет NCS S 4010-R90B	—	—	аналог по характеристикам	шт.	2	—	пом. 3
Т13**	Полотенца для рук вафельные, молочные, на нижних перекладинах сушителя; хлопок 100 %; цвет Tikkurila G503	—	—	аналог по характеристикам	шт.	2	—	пом. 3

Допущения и предложения на листе

Основа листа: размеры сняты с плана заказчика, контрольный обмер не выполнен (К-5); высота потолка 2700 мм принята: на плане заказчика не указана (К-5); подрайон климата не задан — принят не северный (жилые от 2,5 м) (К-4); толщины стен приняты: наружные 250 мм, перегородки 120 мм — не обмерены (К-5); разрешённая мощность 15 кВт принята по типовой квартире, технических условий нет (К-6).

Знак «*» — принято, не замерено и не подтверждено (замерить на объекте): ИЗ-4: КВ-2 — длина петли принята по типовому минимуму 3 м; паспорта выбранной модели нет.

Знак «**» — предложение проектировщика, заказчиком не утверждено (согласовать с заказчиком): ИЗ-3: КВ-1 — длина петли принята по типовому минимуму 3 м; паспорта выбранной модели нет Внутренний блок перенесён со стены А (offset 3300…4200 — внутри оконного проёма 3200…4800) на стену Г, offset 300…1200 (простенок у окна 1, поток вдоль помещения к дивану); наружный блок КН-1 — в простенок между окнами (стена А, 2400…3200); ИЗ-4: Т1, Т2, Т3, Т4, Т5, Т6, Т7, Т8, Т9, Т10, Т11; ИЗ-5: Т12, Т13.

См. лист открытых вопросов (лист 6, записи К-4–К-6; лист 7, записи ИЗ-3–ИЗ-5).

Изм.	Кол.уч	Лист	№ док.	Подп.	Дата
Разраб.		Кырлан А.С.			14.11.26
Пров.					
ГИП					
Н. контр.					
Утв.					

ГД-2026-006-АИ

Квартира 58 м²

Общая площадь 55,23* м² · * размеры приняты, не замерены (реестр — л. 6, 7, К-5)

Дизайн-проект интерьера

Стадия	Лист	Листов
РП	26	108

Спецификация мебели и оборудования (продолжение)

М б/м

Кырлан Александр Сергеевич

Спецификация мебели и оборудования (продолжение)

Форма 1 ГОСТ 21.110-2013 · позиции мебели — по плану расстановки

ПРЕДВАРИТЕЛЬНО · не для производства работ · открыто пунктов: 9 (реестр — л. 6, 7)

Поз.	Наименование и техническая характеристика	Тип, марка, обозначение документа, опросного листа	Код продукции	Поставщик	Ед. измерения	Кол.	Масса 1 ед., кг	Примечание
Т14**	Ковёр — коврик для ванной у бортика ванны, хлопок тафтинг, пыльный синий; хлопок 100 %, латексная противоскользящая основа; цвет NCS S 4010-R90B; 800×450 мм	—	—	аналог по характеристикам	шт.	1	—	пом. 3; с подложкой
	Декор							
ДК1**	Постер над диваном, левый: графика тушью в паспарту, дубовая рама 600×800; 600×800 мм; низ на 1050 мм от пола	—	—	аналог по характеристикам	шт.	1	3	пом. 1; крепление: дюбель с крюком, 2 точки
ДК2**	Постер над диваном, правый: гуашь в паспарту, дубовая рама 600×800; 600×800 мм; низ на 1050 мм от пола	—	—	аналог по характеристикам	шт.	1	3	пом. 1; крепление: дюбель с крюком, 2 точки
ДК3**	Фикус каучуконосный в напольном керамическом кашпо Ø400, матовый белый; 450×450 мм	—	—	аналог по характеристикам	шт.	1	—	пом. 1
ДК4**	Ваза керамическая с веткой эвкалипта на обеденном столе, матовая глазурь, пыльный синий; 200×300 мм; на М3	—	—	аналог по характеристикам	шт.	1	—	пом. 1
ДК5**	Картина над кроватью: акварель в паспарту, дубовая рама 1100×700; 1100×700 мм; низ на 1200 мм от пола	—	—	аналог по характеристикам	шт.	1	4	пом. 2; крепление: дюбель с крюком, 2 точки
ДК6**	Зеркало в рост в тонкой дубовой раме 600×1600; 600×1600 мм; низ на 300 мм от пола	—	—	аналог по характеристикам	шт.	1	12	пом. 2; крепление: анкер для пустотелых оснований, 4 шт.
ДК7**	Замиокулькас в напольном кашпо Ø350, керамика; 400×400 мм	—	—	аналог по характеристикам	шт.	1	—	пом. 2
ДК8**	Зеркало над умывальником, влагостойкое, в тонкой дубовой раме 450×650; 450×650 мм; низ на 1150 мм от пола	—	—	аналог по характеристикам	шт.	1	5	пом. 3; крепление: клей для зеркал + 2 опорных уголка снизу
ДК9**	Постер в тонкой чёрной раме 300×400: линейный рисунок; рама — чёрный матовый; 300×400 мм; центр на 1500 мм от пола	—	—	аналог по характеристикам	шт.	1	1	пом. 4; крепление: дюбель с крюком, 1 точка
ДК12**	Ваза-бутыль керамическая, шалфей, с сухой веткой эвкалипта — на полке короба инсталляции; 130×400 мм	—	—	аналог по характеристикам	шт.	1	—	пом. 4
ДК13**	Свеча в янтарном стекле и аромадиффузор с ротанговыми палочками на подносе — на полке короба; 150×180 мм	—	—	аналог по характеристикам	шт.	1	—	пом. 4
ДК10**	Зеркало в рост в дубовой раме 600×1700; 600×1700 мм; низ на 300 мм от пола	—	—	аналог по характеристикам	шт.	1	12	пом. 5; крепление: анкер для пустотелых оснований, 4 шт.
ДК11**	Постер между дверями: линогравюра, дубовая рама 400×560; 400×560 мм; центр на 1500 мм от пола	—	—	аналог по характеристикам	шт.	1	2	пом. 5; крепление: дюбель с крюком, 2 точки

Допущения и предложения на листе

Основа листа: размеры сняты с плана заказчика, контрольный обмер не выполнен (К-5); высота потолка 2700 мм принята: на плане заказчика не указана (К-5); подрайон климата не задан — принят не северный (жилые от 2,5 м) (К-4); толщины стен приняты: наружные 250 мм, перегородки 120 мм — не обмерены (К-5); разрешённая мощность 15 кВт принята по типовой квартире, технических условий нет (К-6).

Знак «**» — предложение проектировщика, заказчиком не утверждено (согласовать с заказчиком): ИЗ-4: ДК1, ДК2, ДК3, ДК4, ДК5, ДК6, ДК7, ДК8, ДК9, ДК10, ДК11; ИЗ-5: Т14, ДК12, ДК13.

См. лист открытых вопросов (лист 6, записи К-4–К-6; лист 7, записи ИЗ-4, ИЗ-5).

Изм.	Кол.уч	Лист	№ док.	Подп.	Дата
Разраб.		Кырлан А.С.			14.11.26
Пров.					
ГИП					
Н. контр.					
Утв.					

ГД-2026-006-АИ

Квартира 58 м²

Общая площадь 55,23* м² · * размеры приняты, не замерены (реестр — л. 6, 7, К-5)

Дизайн-проект интерьера

Стадия	Лист	Листов
РП	27	108

Спецификация мебели и оборудования (продолжение)

М б/м

Кырлан Александр Сергеевич

03


Электрооборудование

Кырлан Александр Сергеевич

План розеток и электровыводов

Розетки, выводы кабеля, щит · размеры в мм · высоты от чистого пола

План розеток (М 1:50)

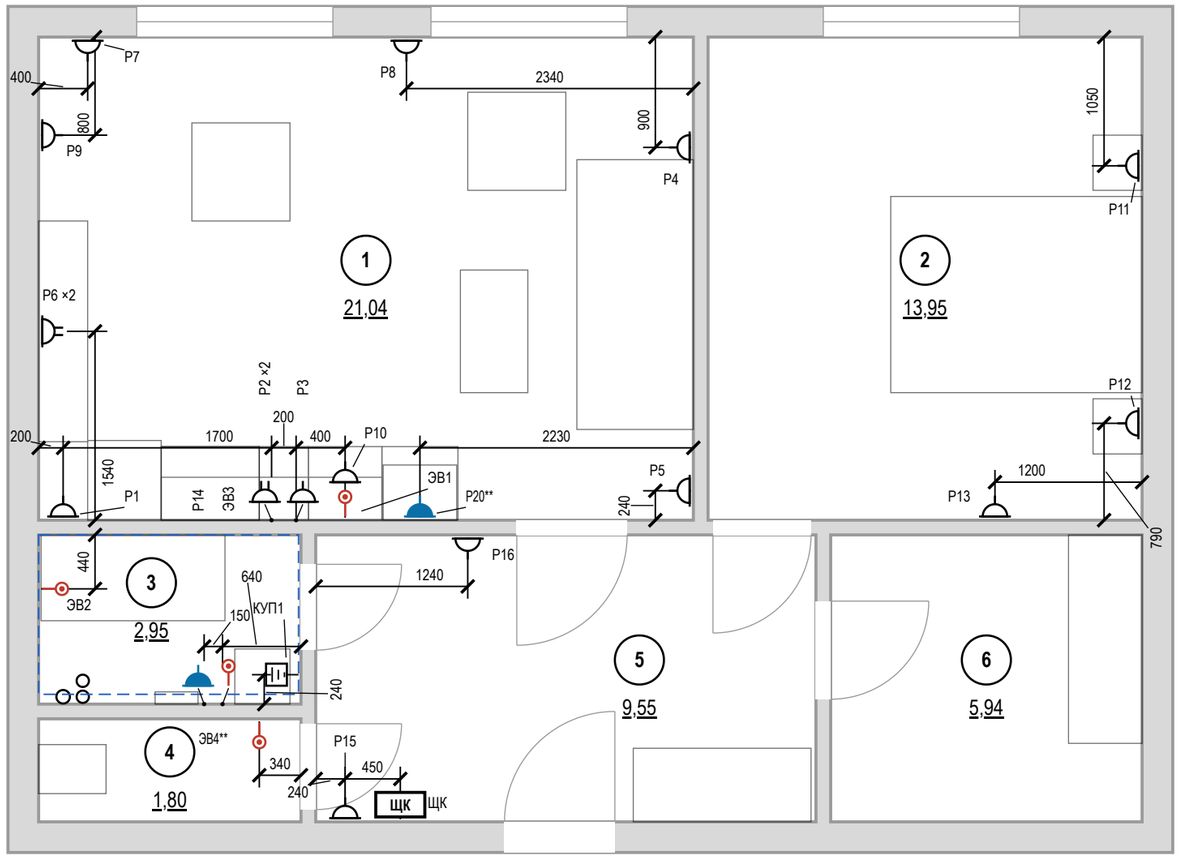

Условные обозначения

Знак	Тип изделия	Н, мм	Кол., шт
	Розетка с заземлением	300	9
	То же	у знака	4
	Блок розеток с заземлением, рамка 2 поста	у знака	2
	Розетка с заземлением IP44	1100	2
	Вывод кабеля к прибору	у знака	4
	КУП (уравнивание потенциалов)	300	1
ЩК	Щит квартирный	1700	1

розетка с заземляющим контактом; у знака — марка и ×N — число постов в рамке; группа щита, высота оси и назначение — в ведомости точек

знак разведён для читаемости: точка на стене — у выноски, привязка — до неё

граница зоны 2 ванной (600 мм от ванны/поддона)

мебель и сантехприборы — подложка

стояк: К1 — канализация, В1 — ХВС, Т3 — ГВС

1 — номер помещения, площадь м²

Итого розеток (механизмов) — 19 шт; рамок — 17 шт: на 1 пост — 15, на 2 поста — 2.

Допущения и предложения на листе

Основа листа: размеры сняты с плана заказчика, контрольный обмер не выполнен (К-5); высота потолка 2700 мм принята: на плане заказчика не указана (К-5); подрайон климата не задан — принят не северный (жилые от 2,5 м) (К-4); толщины стен приняты: наружные 250 мм, перегородки 120 мм — не обмерены (К-5); разрешённая мощность 15 кВт принята по типовой квартире, технических условий нет (К-6).

Знак «**» — предложение проектировщика, заказчиком не утверждено (согласовать с заказчиком): ЭВ4 — вывод к бытовому вентилятору, таймер выбега; К-7: Р20 — питание стиральной машины П6 — отдельная группа 6 (УЗО 30 мА); над столешницей в габарите машины, не за корпусом.

См. лист открытых вопросов (лист 6, записи К-4–К-7).

Примечания

1. За отметку 0,000 принят уровень чистого пола. Высоты Н — от чистого пола до оси изделия; привязки — от чистовой грани стены до оси механизма (у рамки на несколько постов — до оси рамки).
2. Высоты Н и группы щита — в ведомости электроточек: розетки — 300 мм от чистого пола до оси механизма, если в ведомости не указано иное; выводы кабеля — по паспорту прибора.
3. Розетки в санузле — только вне зон 0–2 (ПУЭ 7.1.48, ГОСТ Р 50571.7.701-2024), IP44, через УЗО 30 мА.
4. Розеточные и мокрые линии — через УЗО или дифавтомат с током утечки не более 30 мА (ПУЭ 7.1.79); в санузле выполнить ДСУП (ПУЭ 7.1.87–7.1.88).
5. Кабель — медный, исполнение нг(А)-LS (ГОСТ 31565-2012); скрытая прокладка только горизонтально и вертикально, фактические трассы зафиксировать исполнительной схемой до закрытия отделкой.
6. Расчёт нагрузок, токов КЗ, селективности и сечений — по проекту ЭОМ организации с допуском СРО; лист задаёт состав, расположение и группы.
7. Выводы кухонной техники — после утверждения проекта кухни (ориентировочно); привязки выводов даны от осей модулей гарнитура и пересматриваются вместе с проектом кухни.
8. Ведомости электроточек, изделий, светильников и расшифровка клавиш — лист 31.

1000 мм · печать 1:1

Изм.	Кол.уч	Лист	№ док.	Подп.	Дата
Разраб.		Кырлан А.С.			14.11.26
Пров.					
ГИП					
Н. контр.					
Утв.					

ГД-2026-006-АИ

Квартира 58 м²

Общая площадь 55,23* м² · * размеры приняты, не замерены (реестр — л. 6, 7, К-5)

Дизайн-проект интерьера

Стадия	Лист	Листов
РП	28	108

План розеток и электровыводов

М 1:50

Кырлан Александр Сергеевич


ПРЕДВАРИТЕЛЬНО · не для производства работ · открыто пунктов: 9 (реестр — л. 6, 7)

выпуск 14.11.2026 № bcee049e32 · стр. 31 из 128

План освещения

Светильники, группы включения, извещатели · размеры в мм

План освещения (М 1:50)

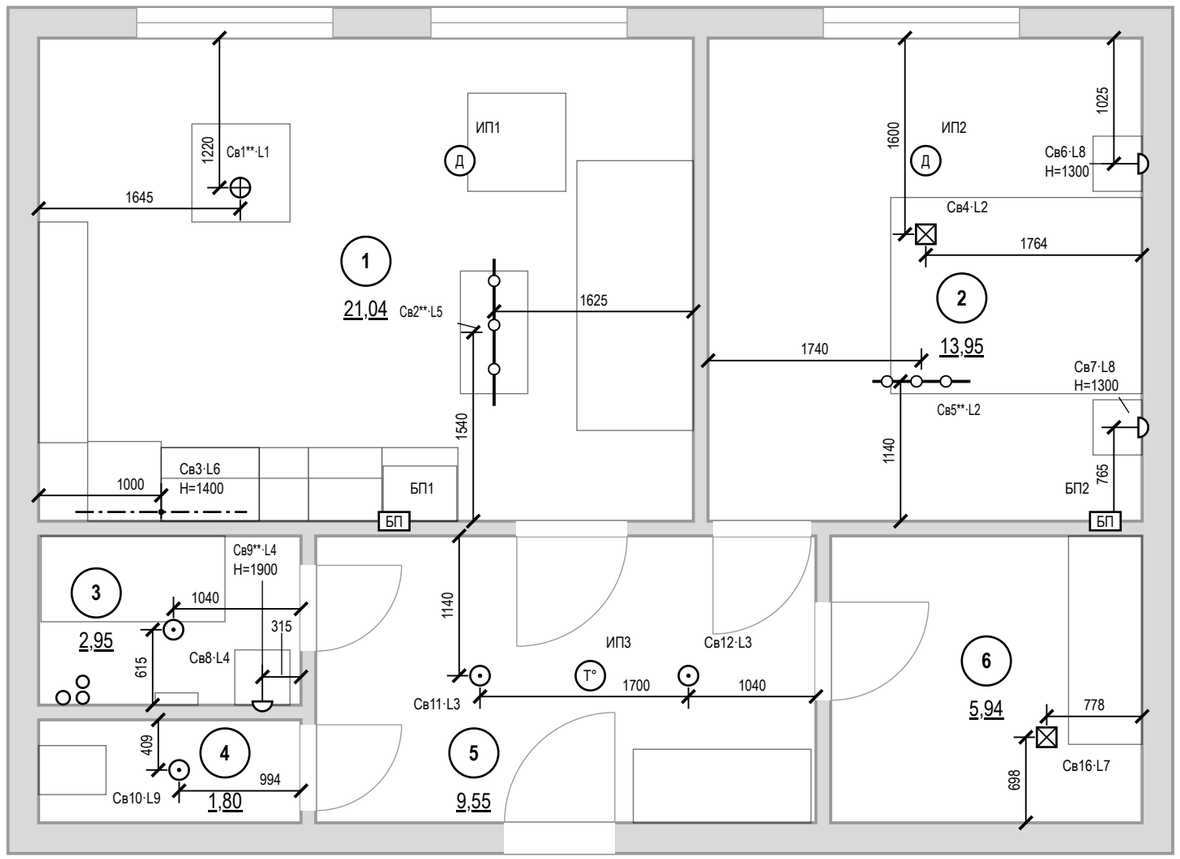

Допущения и предложения на листе

Основа листа: размеры сняты с плана заказчика, контрольный обмер не выполнен (К-5); высота потолка 2700 мм принята: на плане заказчика не указана (К-5); подрайон климата не задан — принят не северный (жилые от 2,5 м) (К-4); толщины стен приняты: наружные 250 мм, перегородки 120 мм — не обмерены (К-5); разрешённая мощность 15 кВт принята по типовой квартире, технических условий нет (К-6).

Знак «**» — предложение проектировщика, заказчиком не утверждено (согласовать с заказчиком): Св2 — общий свет зоны гостиной над журнальным столом М21 (трек шёл вдоль края стола М3 по проходу); трековая система 4 × 950 лм: поток принят до нормы освещённости, модель и паспорт не выбраны; Св5 — трековая система 2 × 900 лм: светильник добавлен проектировщиком, поток принят до нормы освещённости, модель и паспорт не выбраны; Св1 — подвес висел над проходом без заданной высоты, а стол — без света над ним: подвес по оси стола М3; Св9 — свет у зеркала — над зеркалом у умывальника по его оси (свет на лицо, а не над сантехникой).

См. лист открытых вопросов (лист 6, записи К-4–К-6).

Примечания

1. За отметку 0,000 принят уровень чистого пола. Высоты Н — от чистого пола до оси изделия; привязки — от чистовой грани стены до оси механизма (у рамки на несколько постов — до оси рамки).
2. Высота установки, не указанная на плане: светильники — на потолке; настенные — по отметке Н у знака. Привязки — до оси светильника от чистовой грани стены, по рядам.
3. Во влажных помещениях — светильники не ниже IP44; в зонах 0–2 ванной — по ГОСТ Р 50571.7.701-2024 (зона 1 — IPX5).
4. Розеточные и мокрые линии — через УЗО или дифавтомат с током утечки не более 30 мА (ПУЭ 7.1.79); в санузле выполнить ДСУП (ПУЭ 7.1.87–7.1.88).
5. Кабель — медный, исполнение нг(А)-LS (ГОСТ 31565-2012); скрытая прокладка только горизонтально и вертикально, фактические трассы зафиксировать исполнительной схемой до закрытия отделкой.
6. Расчёт нагрузок, токов КЗ, селективности и сечений — по проекту ЭОМ организации с допуском СРО; лист задаёт состав, расположение и группы.
7. Ведомость светильников (тип, количество, мощность, поток, Тц, Ra) — лист 47.
8. Оценка освещённости (по норме СанПиН 1.2.3685-21, табл. 5.52, на полу; не светотехнический расчёт, декоративная подсветка в оценку не входит) — лист 31.

1000 мм · печать 1:1

Условные обозначения

- светильник встраиваемый точечный
- светильник потолочный накладной
- светильник подвесной
- светильник настенный (бра), Н — высота оси
- линейный светильник настенный (подсветка столешницы), точка — вывод питания
- трековая система
- Св1·L1 — марка светильника (как в ведомости и на развёртках) · группа включения L (лист 30)
- Д — извещатель пожарный дымовой автономный
- T° — извещатель пожарный тепловой
- БП — блок питания LED, с доступом (люк от 100×100 мм)
- мебель и сантехприборы — подложка
- стояк: К1 — канализация, В1 — ХВС, Т3 — ГВС
- 1 — номер помещения, площадь м²

Изм.	Кол.уч	Лист	№ док.	Подп.	Дата
Разраб.		Кырлан А.С.			14.11.26
Пров.					
ГИП					
Н. контр.					
Утв.					

ГД-2026-006-АИ

Квартира 58 м²

Общая площадь 55,23* м² · * размеры приняты, не замерены (реестр — л. 6, 7, К-5)

Дизайн-проект интерьера

Стадия	Лист	Листов
РП	29	108

План освещения


М 1:50

Кырлан Александр Сергеевич

План выключателей и схема включения

Выключатели S, группы включения L, линии связи · размеры в мм

План выключателей (М 1:50)

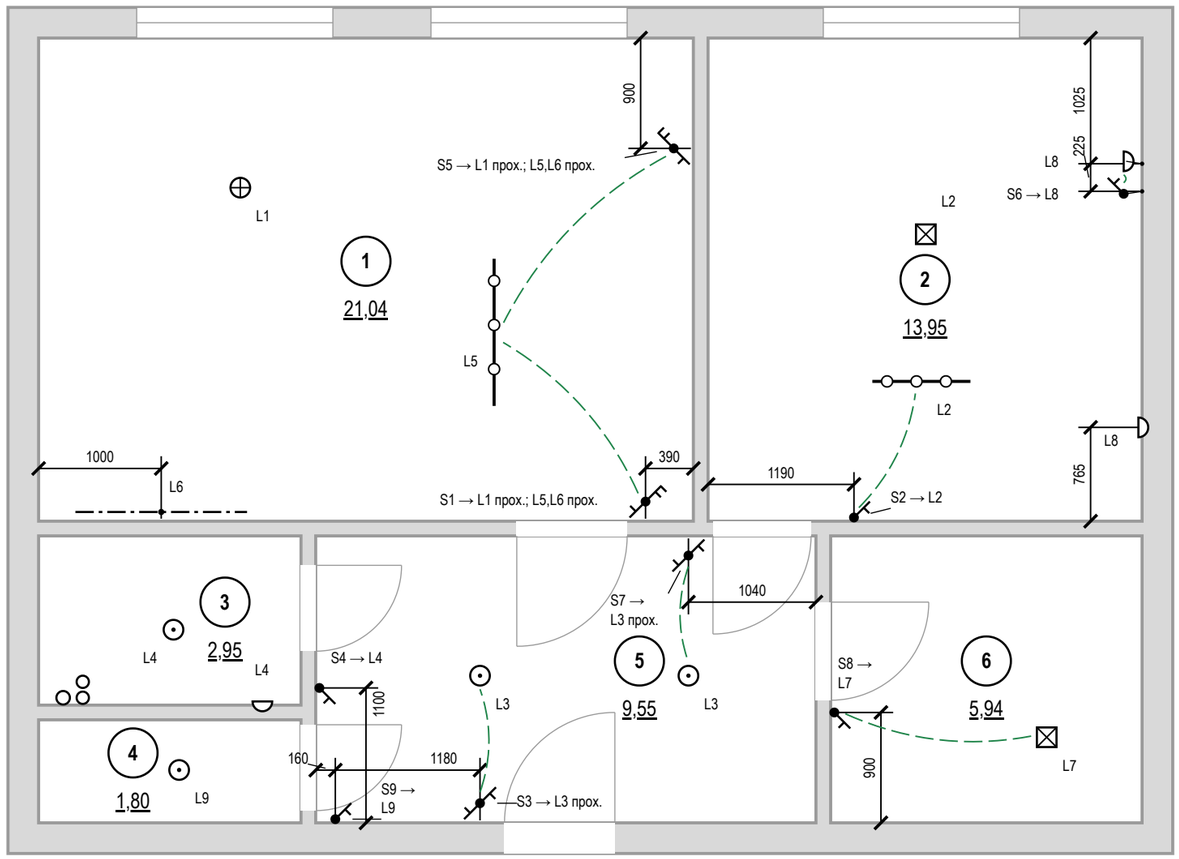

Допущения и предложения на листе

Основа листа: размеры сняты с плана заказчика, контрольный обмер не выполнен (К-5); высота потолка 2700 мм принята: на плане заказчика не указана (К-5); подрайон климата не задан — принят не северный (жилые от 2,5 м) (К-4); толщины стен приняты: наружные 250 мм, перегородки 120 мм — не обмерены (К-5); разрешённая мощность 15 кВт принята по типовой квартире, технических условий нет (К-6).

См. лист открытых вопросов (лист 6, записи К-4–К-6).

Примечания

1. За отметку 0,000 принят уровень чистого пола. Высоты Н — от чистого пола до оси изделия; привязки — от чистовой грани стены до оси механизма (у рамки на несколько постов — до оси рамки).
2. Высота установки, не указанная на плане: выключатели — 900 мм от чистого пола (у кровати и другие — Н у марки), со стороны дверной ручки (ПУЭ 7.1.51).
3. Какой выключатель какие светильники включает — по номеру группы L: у выключателя (S1 → L1; L2 — клавиши по порядку) и у каждого светильника. Пунктир подсказка к ближайшему светильнику группы в том же помещении (не дальше 3 м), это не трасса кабеля; выключатель за стеной (у двери санузла) и далёкая группа — только номер группы.
4. Группы из нескольких мест (L1 — S1, S5; L5 — S1, S5; L6 — S1, S5; L3 — S3, S7): на крайних местах — проходные клавиши, на промежуточных — перекрёстные; механизмы — в ведомости изделий.
5. Вентиляторы санузлов (выводы ЭВ на плане розеток) включаются вместе с основным светом помещения, отключаются с задержкой — таймер выбега в вентиляторе.
6. Розеточные и мокрые линии — через УЗО или дифавтомат с током утечки не более 30 мА (ПУЭ 7.1.79); в санузле выполнить ДСУП (ПУЭ 7.1.87–7.1.88).
7. Кабель — медный, исполнение нг(А)-LS (ГОСТ 31565-2012); скрытая прокладка только горизонтально и вертикально, фактические трассы зафиксировать исполнительной схемой до закрытия отделкой.
8. Расчёт нагрузок, токов КЗ, селективности и сечений — по проекту ЭОМ организации с допуском СРО; лист задаёт состав, расположение и группы.
9. Расшифровка клавиш и ведомость изделий — лист 31.

1000 мм · печать 1:1

Условные обозначения

- выключатель одноклавишный
- выключатель с проходной или перекрёстной клавишей (обратный флажок); тип клавиши — в подписи
- S1 → — марка → группы по клавишам (через «;»): прох. — проходной, перекр. — перекрёстный, дим. — светорегулятор; Н — высота
- связь: выключатель → ближайший светильник группы в том же помещении (не трасса кабеля); полный состав группы — по номеру L
- светильник встраиваемый точечный
- светильник потолочный накладной
- светильник подвесной
- светильник настенный (бра), Н — высота оси
- линейный светильник настенный (подсветка столешницы), точка — вывод питания
- трековая система
- L1 — группа включения у светильника
- стояк: К1 — канализация, В1 — ХВС, Т3 — ГВС
- 1 — номер помещения, площадь м²

Изм.	Кол.уч	Лист	№ док.	Подп.	Дата
Разраб.		Кырлан А.С.			14.11.26
Пров.					
ГИП					
Н. контр.					
Утв.					

ГД-2026-006-АИ

Квартира 58 м²

Общая площадь 55,23* м² · * размеры приняты, не замерены (реестр — л. 6, 7, К-5)

Дизайн-проект интерьера

Стадия	Лист	Листов
РП	30	108

План выключателей и схема включения

М 1:50

Кырлан Александр Сергеевич

выпуск 14.11.2026 № bcee049e32 · стр. 33 из 128

Ведомость электроточек и изделий

Электроточки, изделия, светильники, освещённость, клавиши выключателей · б/м

Ведомость электроточек

Марка	Пом.	Назначение	Н, мм	Гр.
Р1	1	холодильник	300	2
Р2	1	рабочая зона	1100	2
Р3	1	рабочая зона	1100	2
Р4	1	у дивана	300	4
Р5	1	у дивана	300	4
Р6	1	ТВ, приставка (за тумбой М20)	150	4
Р7	1	торшер	300	4
Р8	1	зона отдыха	300	4
Р9	1	обеденная зона	300	4
Р10	1	вытяжка (встроена в дно М10)	2200	2
Р20**	1	стиральная машина, IP44	1100	6
ЭВ1	1	варочная панель	150	3
Р11	2	розетка общего назначения	600	4
Р12	2	розетка общего назначения	600	4
Р13	2	комод, зарядка	300	4
КУП1	3	КУП	300	
Р14	3	фен, IP44	1100	5
ЭВ2	3	вентилятор ВР2 (клавиша L4, таймер выбега)	2400	1
ЭВ3	3	полотенцесушитель, IP44	1000	5
ЭВ4**	4	вентилятор ВР3 (таймер выбега)	2400	1
Р15	5	питание ЩС** (роутер, ИБП)	300	4
Р16	5	уборка	300	4
ЩК	5	щит квартирный	1700	

Ведомость изделий

Наименование	Марки	Ед.	Кол.
Розетка с з/к и защитными шторками, 16 А	по ведомости точек	шт	17
Розетка IP44 с крышкой, 16 А	Р14, Р20**	шт	2
Выключатель 1-клав.	S2, S4, S6, S8, S9	шт	5
Выключатель 1-клав. проходной	S3, S7	шт	2
Выключатель 2-клав. проходной	S1, S5	шт	2
Рамка 1-постовая	в т. ч. 9 под выключ.	шт	24
Рамка 2-постовая		шт	2
Коробка установочная (подрозетник) Ø68	розетки, выключатели	шт	28
Вывод кабеля под прибор (клеммник)	ЭВ1–ЭВ3	шт	3
Вывод кабеля к вентилятору вытяжки	ЭВ4**	шт	1
Коробка уравнивания потенциалов КУП	КУП1	шт	1
Блок питания LED 24 В, 100 Вт	БП1	шт	1
Блок питания LED 24 В, 60 Вт	БП2	шт	1
Извещатель дымовой автономный	ИП1, ИП2	шт	2
Извещатель тепловой	ИП3	шт	1
Щит квартирный (состав — лист щита)	ЩК	шт	1
Розетка компьютерная RJ45, кат. 6, с рамкой и подрозетником	LAN1, LAN2	шт	2
Розетка телевизионная (коаксиальная) с рамкой и подрозетником	ТВ1	шт	1
Трубка или монитор домофона (поставка домофонной организации)	ДФ1	шт	1
Щит слаботочный ЩС**: корпус, DIN-рейка, розетки 220 В	ЩС**	шт	1
Патч-панель, портов не менее 2		шт	1
Коммутатор, портов не менее 2, из них PoE 0		шт	1
Кабель домофона — тип по системе поставщика (по лучам от ЩС**, запас 10 %)		м	3,4
Кабель коаксиальный RG-6 (75 Ом) к розеткам ТВ (по лучам от ЩС**, запас 10 %)		м	16,3
Кабель U/UTP кат. 5e (LAN, Wi-Fi и камеры по PoE) (по лучам от ЩС**, запас 10 %)		м	30,1

Ведомость светильников

Поз.	Марки	Тип	Кол.	Р, Вт	Ф, лм	IP	Тц/Ra
1	Св1**	подвесной	1	40	3600		3000/90
2	Св2**	трековая система	4	12	950		3000/90
3	Св3	линейный светильник, Н=1400	1	14	1080		3000/90
4	Св4	потолочный накладной	1	36	3200		2700/90
5	Св5**	трековая система	2	12	900		2700/90
6	Св6, Св7	настенный (бра), Н=1300	2	4	250		2700/90
7	Св8	встраиваемый точечный	1	9	700	44	3000/90
8	Св9**	настенный (бра), Н=1900	1	6	400	44	3000/90
9	Св10	встраиваемый точечный	1	6	500	44	3000/90
10	Св11, Св12	встраиваемый точечный	2	9	800		3000/90
11	Св16	потолочный накладной	1	10	900		3000/90

Освещённость (оценка)

Пом.	S, м²	Ен, лк	Ф треб., лм	Ф по пр., лм
1	21	150	8890	7400
2	13,9	150	5890	5000
3	3	50	420	700
4	1,8	50	250	500
5	9,6	50	1350	1600
6	5,9	75	1250	900

Расшифровка клавиш

Марка	Пом.	Н, мм	Клав.	Механизм	Группа: светильники
S1	1	900	1	проходной	L1: Св1**
			2	проходной	L5: Св2**; L6: Св3
S2	2	900	1	обычный	L2: Св4, Св5**
S3	5	900	1	проходной	L3: Св11, Св12
S4	5	900	1	обычный	L4: Св8, Св9**
S5	1	900	1	проходной	L1: Св1**
			2	проходной	L5: Св2**; L6: Св3
S6	2	900	1	обычный	L8: Св6, Св7

Расшифровка клавиш (продолжение)

Марка	Пом.	Н, мм	Клав.	Механизм	Группа: светильники
S7	5	900	1	проходной	L3: Св11, Св12
S8	6	900	1	обычный	L7: Св16
S9	5	900	1	обычный	L9: Св10 + ЭВ4** (вентилятор)

Допущения и предложения на листе. Основа листа: размеры сняты с плана заказчика, контрольный обмер не выполнен (К-5); высота потолка 2700 мм принята: на плане заказчика не указана (К-5); подрайон климата не задан — принят не северный (жилые от 2,5 м) (К-4); толщины стен приняты: наружные 250 мм, перегородки 120 мм — не обмерены (К-5); разрешённая мощность 15 кВт принята по типовой квартире, технических условий нет (К-6). Знак «**» — предложение проектировщика, заказчиком не утверждено (согласовать с заказчиком): Св2 — общий свет зоны гостиной над журнальным столом М21 (трек шёл вдоль края стола М3 по проходу); трековая система 4 × 950 лм: поток принят до нормы освещённости, модель и паспорт не выбраны; Св5 — трековая система 2 × 900 лм: светильник добавлен проектировщиком, поток принят до нормы освещённости, модель и паспорт не выбраны; Св1 — подвес висел над проходом без заданной высоты, а стол — без света над ним: подвес по оси стола М3; Св9 — свет у зеркала — над зеркалом у умывальника по его оси (свет на лицо, а не над сантехникой); ЩС — щит слаботочный: место и состав; ЭВ4 — вывод к бытовому вентилятору, таймер выбега; К-7: Р20 — питание стиральной машины П6 — отдельная группа 6 (УЗО 30 мА); над столешницей в габарите машины, не за корпусом. См. лист открытых вопросов (лист 6, записи К-4–К-7).

Примечания

1. Ведомости сведены с планов розеток, освещения и выключателей; марки, группы и высоты — те же, что у знаков на планах.
2. Механизмы, рамки и светорегуляторы — одной серии; число постов и клавиш сверено с выбранной серией. Перекрёстная клавиша — отдельный механизм серии.
3. Освещённость (оценка) — по норме СанПиН 1.2.3685-21 (табл. 5.52, на полу), не светотехнический расчёт; декоративная подсветка в оценку не входит.
4. За отметку 0,000 принят уровень чистого пола. Высоты Н — от чистого пола до оси изделия; привязки — от чистовой грани стены до оси механизма (у рамки на несколько постов — до оси рамки).
5. Розеточные и мокрые линии — через УЗО или дифавтомат с током утечки не более 30 мА (ПУЭ 7.1.79); в санузле выполнить ДСУП (ПУЭ 7.1.87–7.1.88).
6. Кабель — медный, исполнение нг(А)-LS (ГОСТ 31565-2012); скрытая прокладка только горизонтально и вертикально, фактические трассы зафиксировать исполнительной схемой до закрытия отделкой.
7. Расчёт нагрузок, токов КЗ, селективности и сечений — по проекту ЭОМ организации с допуском СРО; лист задаёт состав, расположение и группы.

Изм.	Кол.уч	Лист	№ док.	Подп.	Дата
Разраб.		Кырлан А.С.			14.11.26
Пров.					
ГИП					
Н. контр.					
Утв.					

ГД-2026-006-АИ

Квартира 58 м²

Общая площадь 55,23* м² · * размеры приняты, не замерены (реестр — л. 6, 7, К-5)

Дизайн-проект интерьера

Стадия	Лист	Листов
РП	31	108


Ведомость электроточек и изделий

М б/м

Кырлан Александр Сергеевич

Однолинейная схема щита

Щит квартирный ЩК · без масштаба

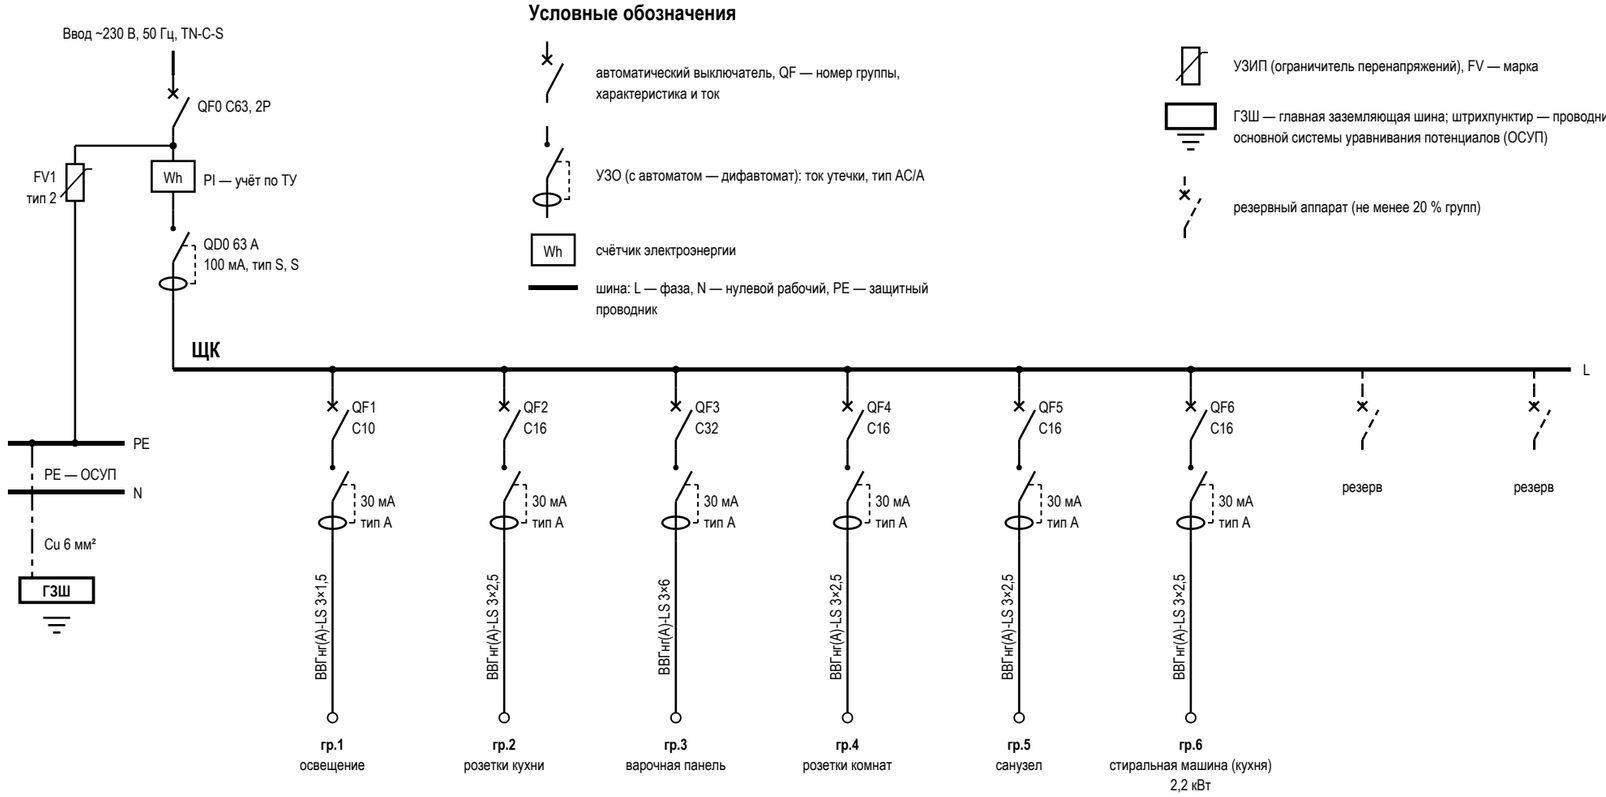

Условные обозначения

- автоматический выключатель, QF — номер группы, характеристика и ток
- УЗО (с автоматом — дифавтомат): ток утечки, тип AC/A
- Wh — счётчик электроэнергии
- шина: L — фаза, N — нулевой рабочий, PE — защитный проводник
- УЗИП (ограничитель перенапряжений), FV — марка
- ГЗШ — главная заземляющая шина; штрихпунктир — проводник основной системы уравнивания потенциалов (ОСУП)
- резервный аппарат (не менее 20 % групп)

Данные щитка

Показатель	Значение
Номер щитка	ЩК
Тип	ЩРВ-П-24, IP41
Уст. мощность, кВт	
Разреш. мощность, кВт	15
Расчётная, кВт	9,8
Автоматы 1п: занят. / рез.	6 / 2
Модулей: всего / занято	24 / 19
Ток на вводе, А	63
Вводной аппарат	QF0 C63, 2P
УЗИП	FV1, тип 2, ЩК, после счётчика
ГЗШ, проводник ОСУП	Cu 6 мм²

Таблица групп щита ЩК и кабельный журнал

№	Назначение	Помещения	Автомат	УЗО / дифавтомат	Кабель	Длина, м	Р, кВт	Точек
1	освещение	1, 2, 3, 4, 5, 6	C10	30 мА, тип A	ВВГнг(A)-LS 3×1,5	106,5		25
2	розетки кухни	1	C16	30 мА, тип A	ВВГнг(A)-LS 3×2,5	20,8		4
3	варочная панель	1	C32	30 мА, тип A	ВВГнг(A)-LS 3×6	10,7		1
4	розетки комнат	1, 2, 5	C16	30 мА, тип A	ВВГнг(A)-LS 3×2,5	48,1		11
5	санузел	3	C16	30 мА, тип A	ВВГнг(A)-LS 3×2,5	12		2
6	стиральная машина (кухня)	1	C16	30 мА, тип A	ВВГнг(A)-LS 3×2,5	11	2,2	1
	Итого по сечениям ВВГнг(A)-LS, м: 3×1,5 — 106,5; 3×2,5 — 91,9; 3×6 — 10,7					209,1		

Примечания

1. Схема однолинейная: одна линия — фаза, N и PE группы; аппараты — в отключённом положении (ГОСТ 2.702, ГОСТ 2.755). Номера групп — как у точек на планах (гр.). За отметку 0,000 принят уровень чистого пола; высота щита — по плану розеток.
2. Розеточные и мокрые линии — через УЗО или дифавтомат с током утечки не более 30 мА (ПУЭ 7.1.79); в санузле выполнить ДСУП (ПУЭ 7.1.87–7.1.88).
3. УЗО тип A — для линий с электроникой, стиральной и посудомоечной машиной, LED-драйверами; тип AC — только для чисто активной нагрузки.
4. Кабель — медный, исполнение нг(A)-LS (ГОСТ 31565-2012); скрытая прокладка только горизонтально и вертикально, фактические трассы зафиксировать исполнительной схемой до закрытия отделкой.
5. Номинал автомата — не выше допустимого тока кабеля: 1,5 мм² — до 10 А, 2,5 мм² — до 16 А. Резерв щита — не менее 20 % модулей.
6. Расчёт нагрузок, токов КЗ, селективности и сечений — по проекту ЭОМ организации с допуском СРО; лист задаёт состав, расположение и группы.
7. УЗИП FV1 — после вводного автомата, проводник к шине PE — кратчайший, без петель. Шина PE щита соединяется с ГЗШ проводником ОСУП; к ГЗШ присоединяются трубы водопровода и отопления на вводе в квартиру (ПУЭ 7.1.87). Шины N и PE — раздельные, после разделения PEN не объединяются.
8. До подключения нагрузки — приёмо-сдаточные испытания с протоколом: сопротивление изоляции линий не менее 0,5 МОм, срабатывание УЗО по току и времени, непрерывность защитных проводников PE (ПУЭ, гл. 1.8).

Допущения и предложения на листе

Основа листа: размеры сняты с плана заказчика, контрольный обмер не выполнен (К-5); высота потолка 2700 мм принята: на плане заказчика не указана (К-5); подрайон климата не задан — принят не северный (жилые от 2,5 м) (К-4); толщины стен приняты: наружные 250 мм, перегородки 120 мм — не обмерены (К-5); разрешённая мощность 15 кВт принята по типовой квартире, технических условий нет (К-6).

Открытые вопросы и конфликты по листу: К-6, К-7.

См. лист открытых вопросов (лист 6, записи К-4–К-7).

Изм.	Кол.уч	Лист	№ док.	Подп.	Дата
Разраб.		Кырлан А.С.			14.11.26
Пров.					
ГИП					
Н. контр.					
Утв.					

ГД-2026-006-АИ

Квартира 58 м²

Общая площадь 55,23* м² · * размеры приняты, не замерены (реестр — л. 6, 7, К-5)

Дизайн-проект интерьера

Стадия	Лист	Листов
РП	32	108

Однолинейная схема щита

М б/м


Кырлан Александр Сергеевич

выпуск 14.11.2026 № bcee049e32 · стр. 35 из 128

План принципиальных трасс

Силовые трассы и объёмы электромонтажа, слаботочка в объёмах · размеры в мм

План принципиальных трасс (М 1:50)

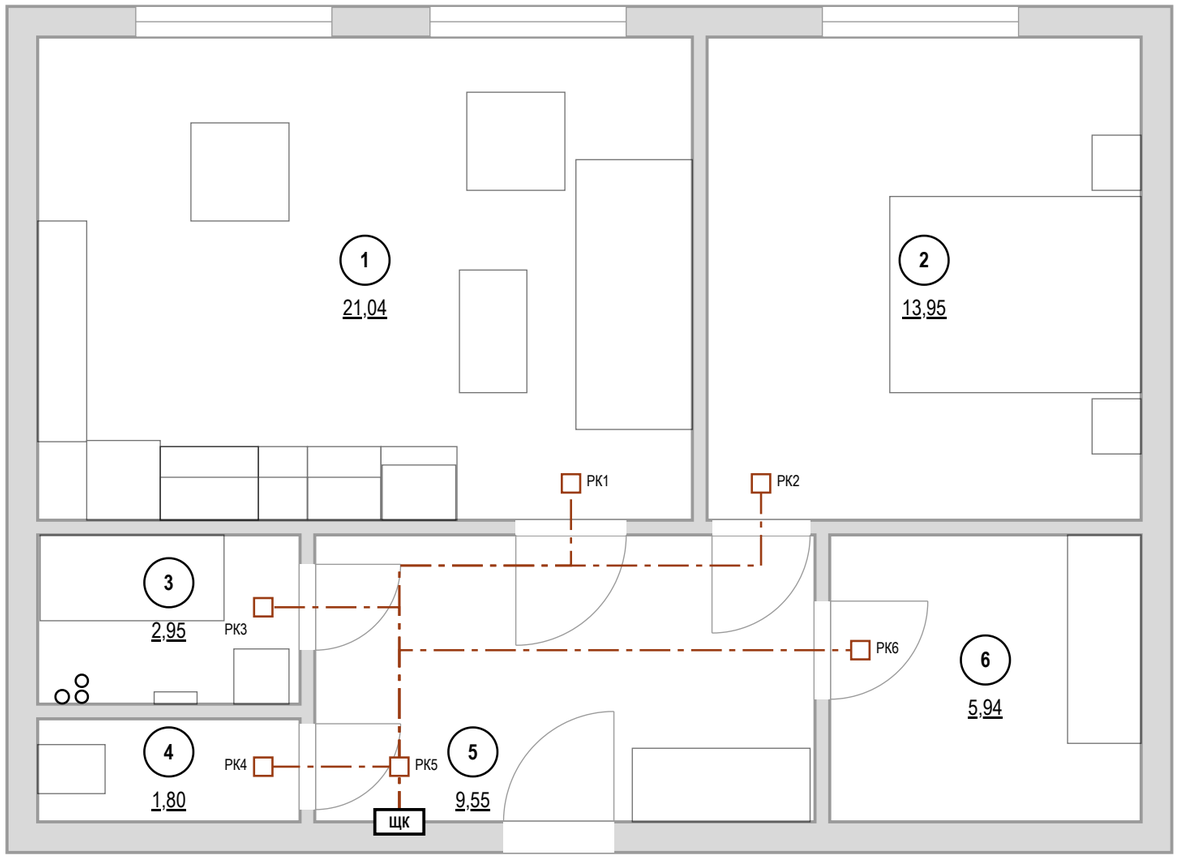

Допущения и предложения на листе

Основа листа: размеры сняты с плана заказчика, контрольный обмер не выполнен (К-5); высота потолка 2700 мм принята: на плане заказчика не указана (К-5); подрайон климата не задан — принят не северный (жилые от 2,5 м) (К-4); толщины стен приняты: наружные 250 мм, перегородки 120 мм — не обмерены (К-5); разрешённая мощность 15 кВт принята по типовой квартире, технических условий нет (К-6).

Знак «**» — предложение проектировщика, заказчиком не утверждено (согласовать с заказчиком): ЩС — щит слаботочный: место и состав.

См. лист открытых вопросов (лист 6, записи К-4–К-6).

Примечания

1. За отметку 0,000 принят уровень чистого пола. Высоты Н — от чистого пола до оси изделия; привязки — от чистовой грани стены до оси механизма (у рамки на несколько постов — до оси рамки).
2. Розеточные и мокрые линии — через УЗО или дифавтомат с током утечки не более 30 мА (ПУЭ 7.1.79); в санузле выполнить ДСУП (ПУЭ 7.1.87–7.1.88).
3. Кабель — медный, исполнение нг(А)-LS (ГОСТ 31565-2012); скрытая прокладка только горизонтально и вертикально, фактические трассы зафиксировать исполнительной схемой до закрытия отделкой.
4. Расчёт нагрузок, токов КЗ, селективности и сечений — по проекту ЭОМ организации с допуском СРО; лист задаёт состав, расположение и группы.
5. Длины — по плану: от щита вверх в потолочное пространство, по дверям и коридору без захода в мокрые помещения к распределительной коробке над дверью, далее к точкам; вертикали считаются вниз и обратно (у последней точки цепочки — в один конец); запас 10 %. Трассы принципиальные: фактическую зафиксировать исполнительной схемой до закрытия отделкой.
6. Несущие стены не определены: штробы в стенах не выполнять. Маршрут проложен без штроб: горизонтали — за потолком в гофре (72,6 м) и в кабель-канале плинтуса (55,8 м), вертикали — в коробе или накладном канале (77,8 м кабеля). Точек: за потолком — 9, спуск из потолка — 7, по плинтусу — 11, плинтус и подъём — 18.
7. Вариант со штробами — работа после технического заключения: 58,99 м вертикальных штроб от потолка до каждой настенной точки; условие — только после технического заключения: стена не несущая (или вертикальная штроба в несущей согласована конструктором), глубина и ширина 20–25 мм, не в зонах 0–2 ванной. Без заключения и согласования конструктора в смету и в график эта работа не входит.
8. Слаботочные сети: кабели и точки считаются по лучам от ЩС** (лист слаботочных сетей): 50 м, портов патч-панели и коммутатора не менее 2. Изделия — в ведомости изделий.

1000 мм · печать 1:1

Кабель по группам ВВГнг(А)-LS, м

Гр.	мм²	Трасса	Данные
1	3×1,5	106,5	
2	3×2,5	20,8	
3	3×6	10,7	

Гр.	мм²	Трасса	Данные
4	3×2,5	48,1	
5	3×2,5	12	
6	3×2,5	11	
Σ		**209,1**	

Экспликация помещений

№	Помещение	Площадь, м²
1	Кухня-гостиная	21,04
2	Спальня	13,95
3	Ванная	2,95
4	Санузел	1,80
5	Прихожая	9,55
6	Гардеробная	5,94
	Итого (общая площадь)	55,23

Объёмы прокладки

Работа, материал	Ед.	Кол.
Гофротруба Ø20 в потолочном пространстве	м	72,6
Кабель-канал плинтуса для силовых линий	м	55,8
Короб или накладной канал для вертикальных спусков и подъёмов	м	44,2
Коробка распределительная (РК) над дверью помещения	шт	6
Слаботочка: кабель домофона	м	3,4
Слаботочка: Кабель коаксиальный RG-6 (75 Ом) к розеткам ТВ	м	16,3
Слаботочка: Кабель U/UTP кат. 5е (LAN, Wi-Fi и камеры по PoE)	м	30,1
Слаботочка: гофротруба Ø20 отдельно от силовых	м	44,8

Штробы — только после заключения

Работа	Ед.	Кол.
Вертикальные штробы 20×20 мм от потолка до каждой настенной точки (в маршрут без штроб не входят)	м	58,99

Условные обозначения

- ЩК — щит квартирный
- РК — распределительная коробка над дверью помещения
- магистраль от щита к РК: потолочное пространство, гофра
- мебель и сантехприборы — подложка

Изм.	Кол.уч	Лист	№ док.	Подп.	Дата
Разраб.		Кырлан А.С.			14.11.26
Пров.					
ГИП					
Н. контр.					
Утв.					

ГД-2026-006-АИ

Квартира 58 м²

Общая площадь 55,23* м² · * размеры приняты, не замерены (реестр — л. 6, 7, К-5)

Дизайн-проект интерьера

Стадия	Лист	Листов
РП	33	108

План принципиальных трасс

М 1:50

Кырлан Александр Сергеевич

выпуск 14.11.2026 № bcee049e32 · стр. 36 из 128

Таблица нагрузок щита

щит ЩК · 6 групп · Ррасч 1,1 кВт · без масштаба

Группы щита ЩК (1)

№	Назначение	Руст, кВт	Кс	Ррасч, кВт	Iрасч, А	Автомат	Кабель
1	освещение	0	0,6	0	0	C10	3×1,5
2	розетки кухни	0	0,4	0	0	C16	3×2,5
3	варочная панель	0	0,6	0	0	C32	3×6

Группы щита ЩК (2)

№	Назначение	Руст, кВт	Кс	Ррасч, кВт	Iрасч, А	Автомат	Кабель
4	розетки комнат	0	0,4	0	0	C16	3×2,5
5	санузел	0	0,7	0	0	C16	3×2,5
6	стиральная машина (кухня)	2,2	0,7	1,54	7	C16	3×2,5

Итог по квартире

Показатель	Значение
Установленная мощность Σ Руст	2,2 кВт
Σ Руст × Кс по группам	1,54 кВт
Коэффициент одновременности	0,7
Расчётная мощность квартиры Ррасч	1,1 кВт
Расчётный ток Iрасч (230 В, cosφ 0,95)	5 А
Разрешённая мощность	15 кВт
Запас до разрешённой	92,8 %
Вводной аппарат	C63, 2P

Примечания

1. Руст — установленная мощность группы по данным щита (приборы — по паспорту, розетки общего назначения — оценка 0,1 кВт на гнездо). Кс — коэффициенты спроса: освещение 0,6; розетки 0,4; варочная и духовой 0,6; кондиционеры 0,8; тёплый пол 1,0; прочие 0,7; одновременность 0,7.
2. Коэффициенты — ориентир исполнителя, не табличные значения нормы; расчёт нагрузки подтверждает инженер ЭОМ (СП 256.1325800.2016). Под разрешённую мощность они не подгоняются.
3. Вывод: запас 93 % (расчётная 1,1 кВт при разрешённой 15 кВт).
4. Розеточные и мокрые линии — через УЗО или дифавтомат с током утечки не более 30 мА (ПУЭ 7.1.79); в санузле выполнить ДСУП (ПУЭ 7.1.87–7.1.88).

Допущения и предложения на листе

Основа листа: размеры сняты с плана заказчика, контрольный обмер не выполнен (К-5); высота потолка 2700 мм принята: на плане заказчика не указана (К-5); подрайон климата не задан — принят не северный (жилые от 2,5 м) (К-4); толщины стен приняты: наружные 250 мм, перегородки 120 мм — не обмерены (К-5); разрешённая мощность 15 кВт принята по типовой квартире, технических условий нет (К-6).

См. лист открытых вопросов (лист 6, записи К-4–К-6).

Изм.	Кол.уч	Лист	№ док.	Подп.	Дата
Разраб.		Кырлан А.С.			14.11.26
Пров.					
ГИП					
Н. контр.					
Утв.					

ГД-2026-006-АИ

Квартира 58 м²

Общая площадь 55,23* м² · * размеры приняты, не замерены (реестр — л. 6, 7, К-5)

Дизайн-проект интерьера

Стадия	Лист	Листов
РП	34	108

Таблица нагрузок щита


М б/м

Кырлан Александр Сергеевич

План слаботочных сетей

Интернет, ТВ, домофон · размеры в мм · высоты от чистого пола

План слаботочных сетей (М 1:50)

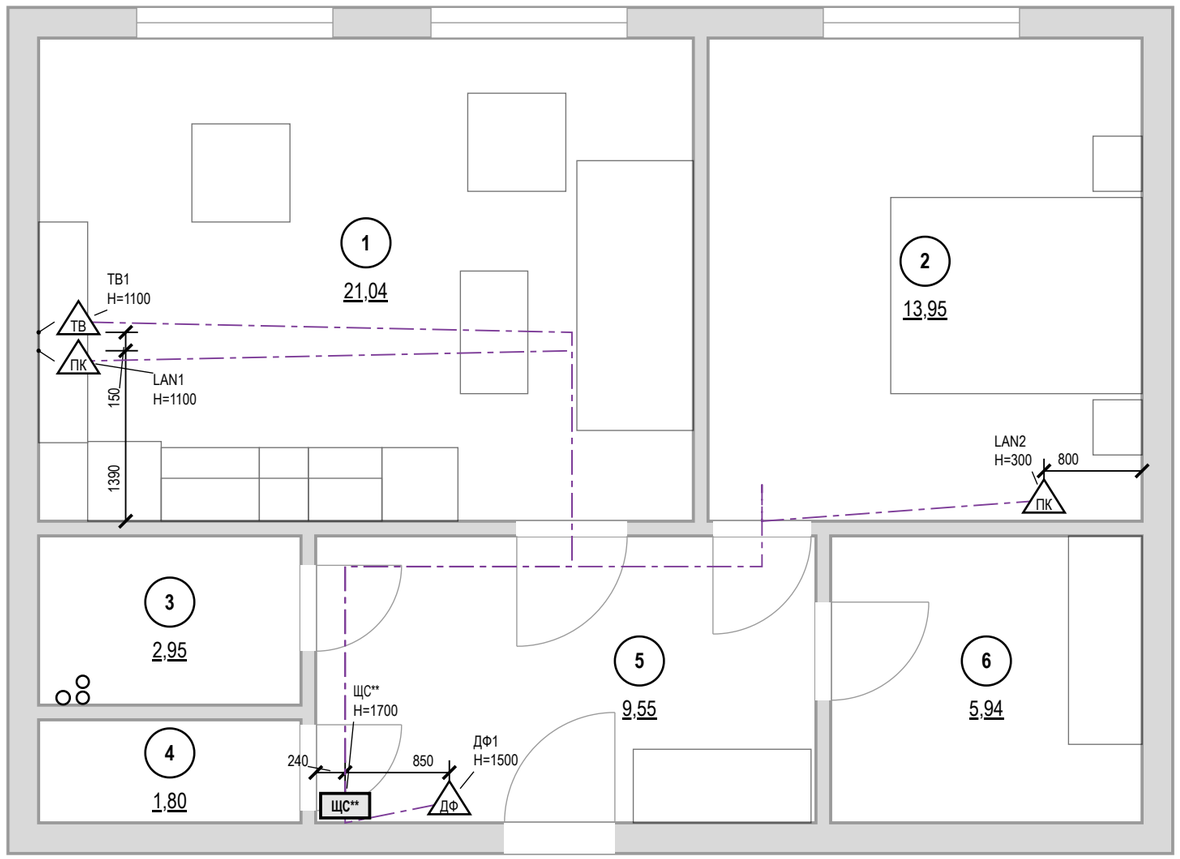

ПРЕДВАРИТЕЛЬНО · не для производства работ · открыто пунктов: 9 (реестр — л. 6, 7)

Ведомость слаботочных точек

Марка	Пом.	Назначение	H, мм	Кабель
ТВ1	1	розетка ТВ	1100	RG-6 (75 Ом)
LAN1	1	розетка LAN (RJ45)	1100	U/UTP кат. 5e/6
LAN2	2	розетка LAN (RJ45)	300	U/UTP кат. 5e/6
ЩС**	5	щит слаботочный	1700	ввод пров.
ДФ1	5	домофон (трубка)	1500	по системе

Условные обозначения

- ЩС — щит слаботочный: ввод провайдера, роутер, коммутатор
- ПК — розетка компьютерная RJ45
- ТВ — розетка телевизионная
- ДФ — трубка или монитор домофона
- кабель от ЩС до точки, отдельным лучом
- мебель и сантехприборы — подложка
- стояк: К1 — канализация, В1 — ХВС, Т3 — ГВС
- 1 — номер помещения, площадь м²

Допущения и предложения на листе

Основа листа: размеры сняты с плана заказчика, контрольный обмер не выполнен (К-5); высота потолка 2700 мм принята: на плане заказчика не указана (К-5); подрайон климата не задан — принят не северный (жилые от 2,5 м) (К-4); толщины стен приняты: наружные 250 мм, перегородки 120 мм — не обмерены (К-5); разрешённая мощность 15 кВт принята по типовой квартире, технических условий нет (К-6).

Знак «**» — предложение проектировщика, заказчиком не утверждено (согласовать с заказчиком): ЩС — щит слаботочный: место и состав.

См. лист открытых вопросов (лист 6, записи К-4–К-6).

Примечания

1. За отметку 0,000 принят уровень чистого пола. Высоты Н — от чистого пола до оси изделия; привязки — от чистовой грани стены до оси механизма (у рамки на несколько постов — до оси рамки).
2. Высота установки, не указанная на плане: розетки LAN и ТВ — 300 мм от чистого пола.
3. Слаботочные кабели — отдельно от силовых: в своей трубе или лотке, при параллельной прокладке не ближе 100 мм к силовым, пересечения под прямым углом; каждую точку — отдельным кабелем от ЩС** без скруток.
4. Трассы на листе — принципиальные; фактические зафиксировать исполнительной схемой до закрытия отделкой. Силовые линии, УЗО 30 мА, ДСУП, кабель нг(А)-LS — по листам розеток и щита.
5. Проект силовой части и расчёт токов КЗ — по проекту ЭОМ; слаботочная часть согласуется с провайдером и управляющей компанией (домофон, коллективное ТВ).

1000 мм · печать 1:1

Изм.	Кол.уч	Лист	№ док.	Подп.	Дата
Разраб.		Кырлан А.С.			14.11.26
Пров.					
ГИП					
Н. контр.					
Утв.					

ГД-2026-006-АИ

Квартира 58 м²

Общая площадь 55,23* м² · * размеры приняты, не замерены (реестр — л. 6, 7, К-5)

Дизайн-проект интерьера

Стадия	Лист	Листов
РП	35	108

План слаботочных сетей

М 1:50

Кырлан Александр Сергеевич

выпуск 14.11.2026 № bcee049e32 · стр. 38 из 128

04

Отопление и вентиляция

Кырлан Александр Сергеевич

выпуск 14.11.2026 bcee049e32 · стр. 39 из 128


План вентиляции

Вытяжка, приток, переток, кондиционеры · размеры в мм · высоты от чистого пола

ПРЕДВАРИТЕЛЬНО · не для производства работ · открыто пунктов: 9 (реестр — л. 6, 7)

План вентиляции (М 1:50)

Допущения и предложения на листе. Основа листа: размеры сняты с плана заказчика, контрольный обмер не выполнен (К-5); высота потолка 2700 мм принята: на плане заказчика не указана (К-5); подрайон климата не задан — принят не северный (жилые от 2,5 м) (К-4); толщины стен приняты: наружные 250 мм, перегородки 120 мм — не обмерены (К-5); разрешённая мощность 15 кВт принята по типовой квартире, технических условий нет (К-6). Знак «*» — принято, не замерено и не подтверждено (замерить на объекте): ИЗ-4: КВ-2 — длина петли принята по типовому минимуму 3 м; паспорта выбранной модели нет. Знак «**» — предложение проектировщика, заказчиком не утверждено (согласовать с заказчиком): ИЗ-3: КВ-1 — длина петли принята по типовому минимуму 3 м; паспорта выбранной модели нет Внутренний блок перенесён со стены А (offset 3300…4200 — внутри оконного проёма 3200…4800) на стену Г, offset 300…1200 (простенок у окна 1, поток вдоль помещения к дивану); наружный блок КН-1 — в простенок между окнами (стена А, 2400…3200). См. лист открытых вопросов (лист 6, записи К-1, К-4–К-6; лист 7, записи ИЗ-3, ИЗ-4); по листу — К-1.

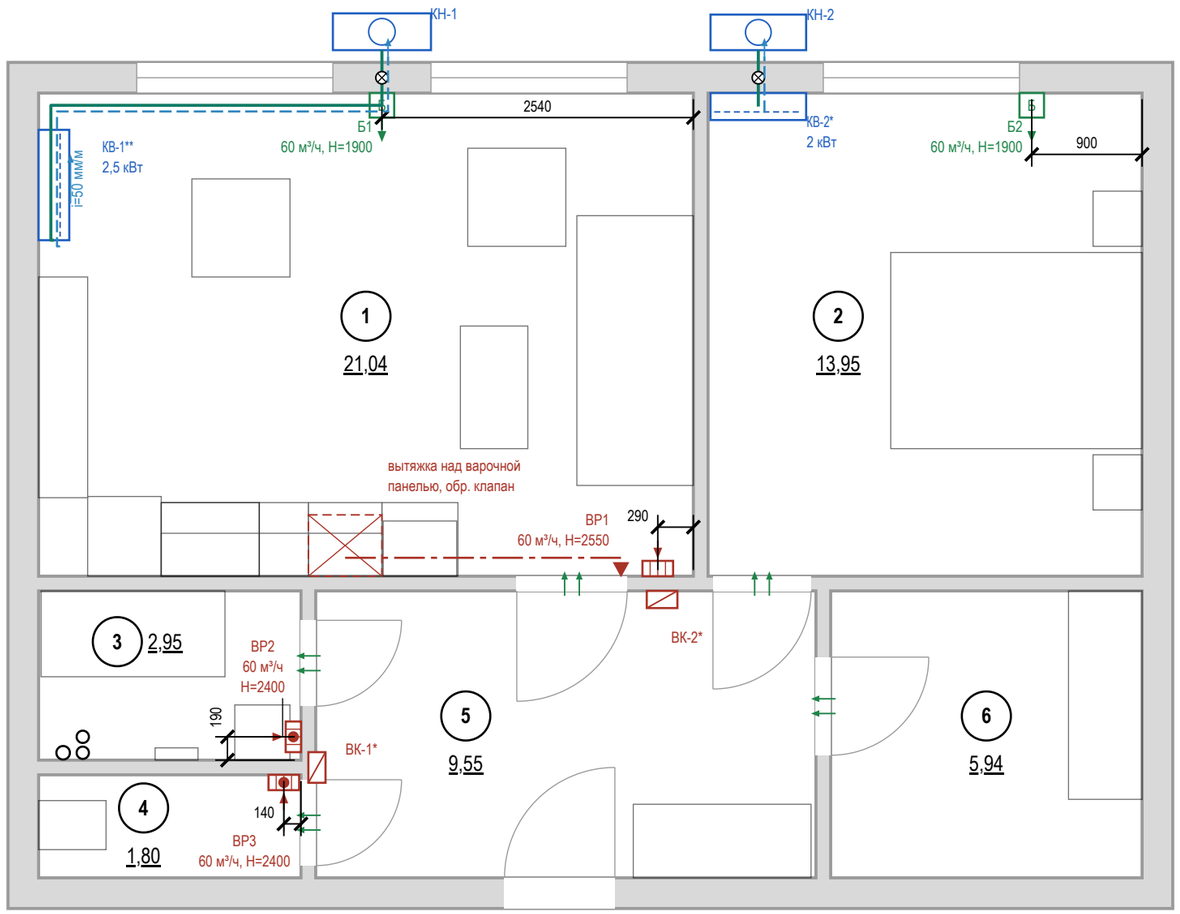

Условные обозначения

- стояк: К1 — канализация, В1 — ХВС, Т3 — ГВС
- номер помещения, площадь м²
- вытяжная решётка в вентканал: марка, расход м³/ч, Н центра от чистого пола
- вытяжная решётка с бытовым вентилятором и обратным клапаном: марка, расход, Н
- бризер (приток с фильтром и подогревом)
- переток: зазор под полотном или переточная решётка
- кухонная вытяжка над варочной панелью
- вентканал ВК-N; «*» — принят до обмера
- воздуховод кухонной вытяжки в коробе под потолком
- отдельный вход воздуховода в вентканал, обратный клапан
- внутренний блок кондиционера (КВ-N)
- наружный блок (КН-N) на фасаде / в корзине
- трасса фреонопровода и межблочного кабеля
- дренаж конденсата (уклон стрелкой)
- отверстие в наружной стене под трассу

Воздухообмен, м³/ч

№	Помещение	Выт. норма	Выт. проект	Прит. норма	Прит. проект	Устрой-ства
1	Кухня-гостиная	60	60	60	60	ВР1, Б1
2	Спальня			60	60	Б2
3	Ванная	50	60			ВР2
4	Санузел	25	60			ВР3
6	Гардеробная	3				переток
	Итого	**138**	**180**	**120**	**120**	
	Норма по жильцам: 30×2			60		

Воздухообмен квартиры — по большей из сумм притока и вытяжки: норма 138 м³/ч, проект 180 м³/ч.
Вытяжка не меньше притока — баланс сведён.

Кондиционеры

Марка	Помещение	Нар. блок	Трасса, м	Дренаж
КВ-1**	1. Кухня-гостиная	КН-1	3,0	наружу, i=50 мм/м
КВ-2*	2. Спальня	КН-2	3,0 п	наружу, i=50 мм/м

Примечания

1. Расчёт систем ОВ и подбор оборудования — проектная организация с допуском СРО; лист даёт места, трассы и привязки.
2. Нормы вытяжки — СП 54.13330.2022 (Изм. 1, 2), табл. 7.1: кухня с электроплитой 60 м³/ч, с газовой 100; ванная и совмещённый санузел 50; уборная 25; гардеробная 0,2 ч⁻¹. Приток в жилые — 3 м³/ч на 1 м² (менее 20 м² общей площади на человека), иначе 30 м³/ч на человека.
3. Вентканалы и шахты не сужать, не переносить и не закрывать; вентилятор и кухонная вытяжка — через обратный клапан, без перекрытия естественной тяги.
4. Кухонная вытяжка в воздухообмен не включена: воздуховод не менее Ø125 в коробе, вход в канал отдельный.
5. Переток — зазор под полотнами межкомнатных дверей или переточная решётка.
6. Дренаж кондиционера — непрерывный уклон 40–60 мм/м без контруклонов (СТО НОСТРОЙ 2.23.1-2011, п. 5.8.4); врезка в К1 — через сифон (п. 5.8.9); длина трассы и перепад высот — по паспорту блока; внутренний блок — не ближе 150 мм к потолку, не над кроватью и рабочим местом.
7. Наружный блок на фасаде многоквартирного дома — с согласия собственников (общее имущество); при наличии корзин — только в них.
8. «п» в графе «Трасса» — трасса фреона по плану короче минимума, разница выбрана компенсационной петлёй (бухтой): КВ-2* — по плану 0,8 м, с петлёй 3,0 м. Длина петли принята по минимуму трассы (3,0 м) и зависит от паспорта модели кондиционера, которая ещё не выбрана: минимум и максимум трассы — типовые, по паспорту модели, до заказа сверить и при необходимости изменить петлю или место наружного блока. Бухту уложить в коробе или за внутренним блоком, не в штробе.
9. Привязки оборудования — по паспортам приобретённых моделей, до черновых работ.
10. Привязки — до обмера: вентканалы ВК-N* приняты проектировщиком, решётки и воздуховоды — от них. До черновых работ — обмер каналов и тяги, лист перевыпустить по факту.

1000 мм · печать 1:1

Изм.	Кол.уч	Лист	№ док.	Подп.	Дата
Разраб.		Кырлан А.С.			14.11.26
Пров.					
ГИП					
Н. контр.					
Утв.					

ГД-2026-006-АИ

Квартира 58 м²

Общая площадь 55,23* м² · * размеры приняты, не замерены (реестр — л. 6, 7, К-5)

Дизайн-проект интерьера

Стадия	Лист	Листов
РП	36	108

План вентиляции

М 1:50


Кырлан Александр Сергеевич

выпуск 14.11.2026 № bcee049e32 · стр. 40 из 128

План отопления

Радиаторы, стояки, подводки · размеры в мм · высоты от чистого пола

План отопления (М 1:50)

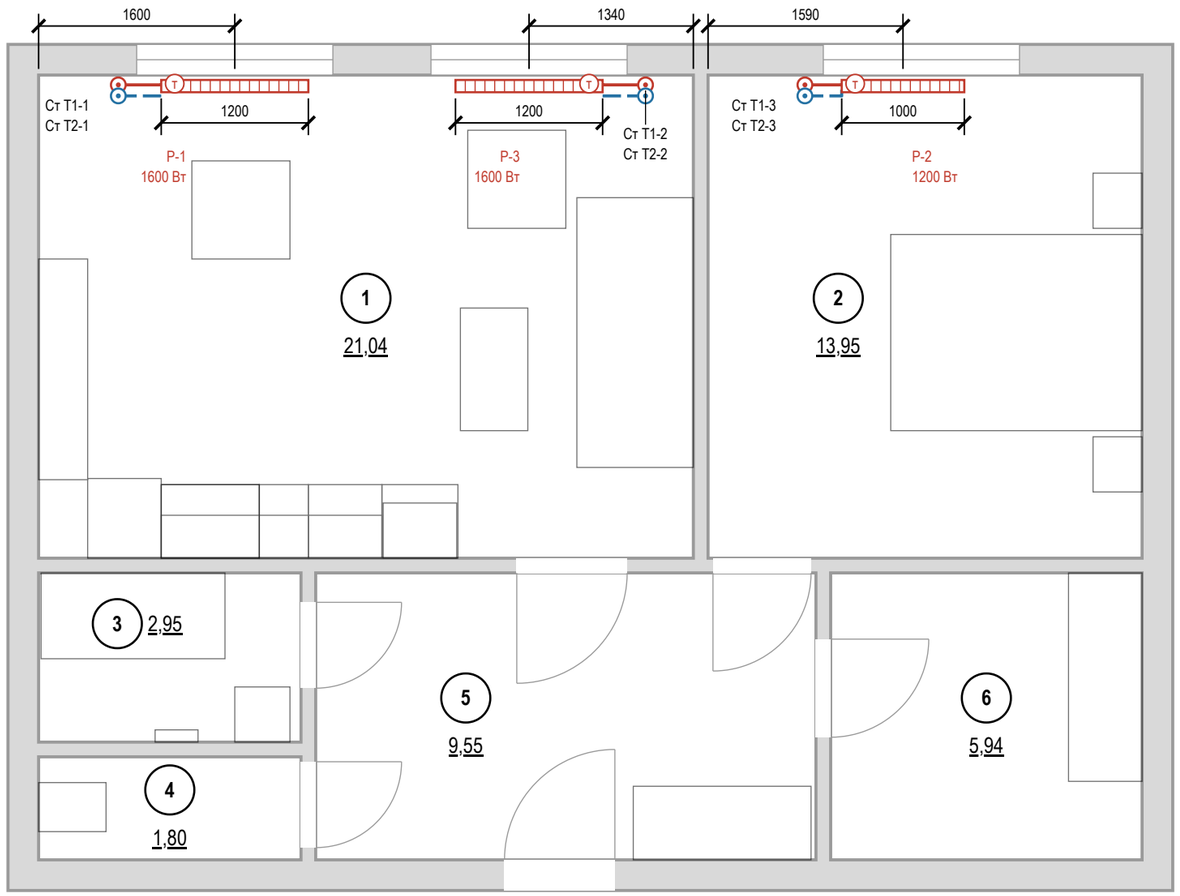

Примечания

1. Расчёт системы отопления, теплопотерь и подбор приборов — проектная организация с допуском СРО; лист даёт места и привязки.
2. Тип, длина и мощность радиаторов — по теплотехническому расчёту; лист задаёт места, зазоры и подключение.
3. Зазоры радиатора: низ не менее 100 мм от чистого пола, верх не менее 100 мм до подоконника, 30–50 мм от стены до задней панели; центр по оси окна с допуском ±20 мм. Верх до подоконника — 180 мм.
4. Радиаторы не закрывать глухими коробами и мебелью; перенос и замена приборов в многоквартирном доме — переустройство, согласование с управляющей организацией (ЖК РФ ст. 25–26); вынос на лоджию запрещён.
5. Трубы отопления через межквартирные стены не прокладывать (СП 51.13330.2011, п. 9.19); через перекрытия и перегородки — в гильзах.
6. Привязки приборов и подводок — по паспортам приобретённых радиаторов и клапанов, до черновых работ.
7. До закрытия отделкой трубопроводы отопления испытать гидростатическим давлением с оформлением акта (СП 73.13330.2016, 7.2–7.3).

Допущения и предложения на листе

Основа листа: размеры сняты с плана заказчика, контрольный обмер не выполнен (К-5); высота потолка 2700 мм принята: на плане заказчика не указана (К-5); подрайон климата не задан — принят не северный (жилые от 2,5 м) (К-4); толщины стен приняты: наружные 250 мм, перегородки 120 мм — не обмерены (К-5); разрешённая мощность 15 кВт принята по типовой квартире, технических условий нет (К-6).

См. лист открытых вопросов (лист 6, записи К-4–К-6).

1000 мм · печать 1:1

ПРЕДВАРИТЕЛЬНО · не для производства работ · открыто пунктов: 9 (реестр — л. 6, 7)

Условные обозначения

- (1) — номер помещения, площадь м²
- радиатор отопления (марка РО-N, длина по плану)
- (Т) — клапан с термоголовкой на подаче
- стояк отопления, подающий (Ст Т1-N)
- стояк отопления, обратный (Ст Т2-N)
- Т1 — отопление, подающий трубопровод
- Т2 — отопление, обратный трубопровод

Ведомость радиаторов

Марка	Помещение	Тип	Д×В×Г, мм	Низ / стена	Q, Вт
Р-1	1. Кухня-гостиная	панельный 22	1200×500×100	120 / 40	1600
Р-3	1. Кухня-гостиная	панельный 22	1200×500×100	120 / 40	1600
Р-2	2. Спальня	панельный 22	1000×500×100	120 / 40	1200

Низ — от чистого пола, стена — зазор до задней панели, мм.

Привязки — до обмера

Стояки отопления в исходных данных не заданы: показаны у откосов окон, подводки — принципиально. До черновых работ — обмер стояков и паспорта приборов; лист перевыпустить по факту.

Изм.	Кол.уч	Лист	№ док.	Подп.	Дата
Разраб.		Кырлан А.С.			14.11.26
Пров.					
ГИП					
Н. контр.					
Утв.					

ГД-2026-006-АИ

Квартира 58 м²

Общая площадь 55,23* м² · * размеры приняты, не замерены (реестр — л. 6, 7, К-5)

Дизайн-проект интерьера

Стадия	Лист	Листов
РП	37	108

План отопления

М 1:50

Кырлан Александр Сергеевич

выпуск 14.11.2026 № bcee049e32 · стр. 41 из 128

05

Водоснабжение и канализация


Кырлан Александр Сергеевич

План выводов сантехники


Выводы В1, Т3**, К1 · привязки от чистовых стен · высоты от чистого пола, мм

ПРЕДВАРИТЕЛЬНО · не для производства работ · открыто пунктов: 9 (реестр — л. 6, 7)


Фрагмент 1. Кухня-гостиная, пом. 1 (М 1:25)

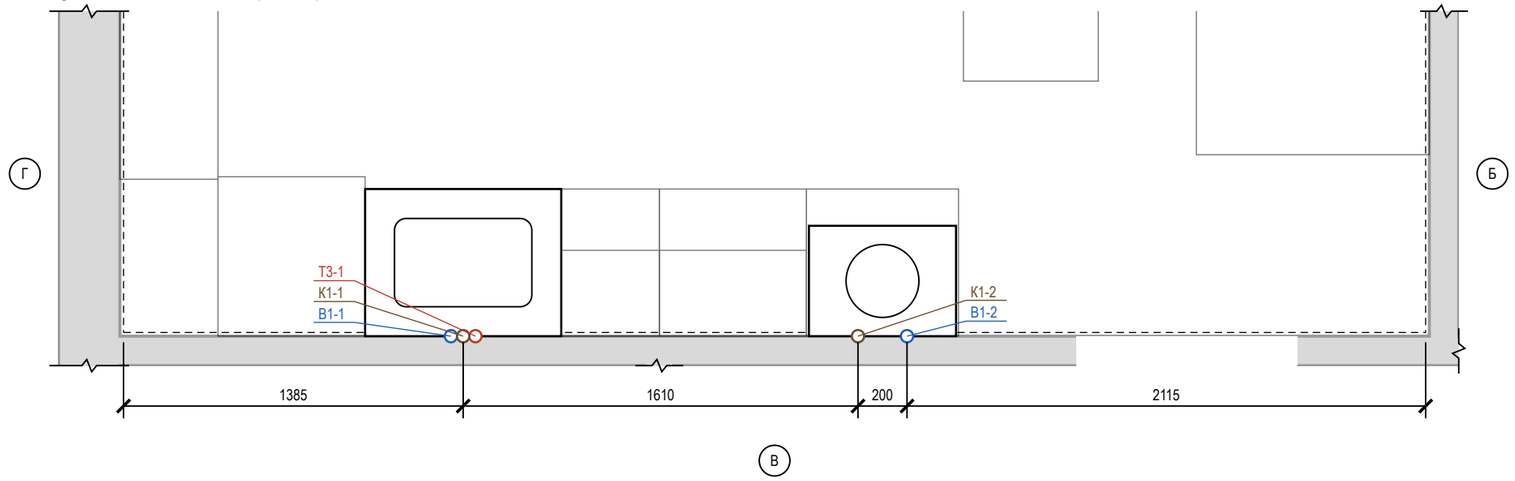

Фрагмент 2. Ванная, пом. 3 (М 1:25)

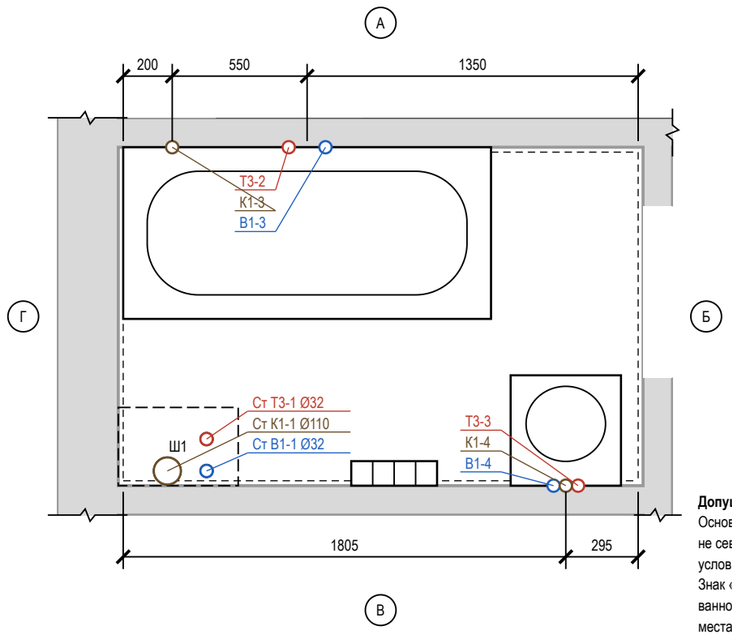

Фрагмент 3. Санузел, пом. 4 (М 1:25)

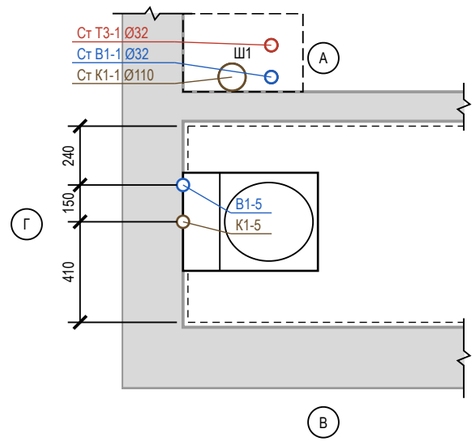

Ведомость привязок выводов

Код	Прибор	Ø	Н, мм	Привязка от чист. стен, мм	Прим.
В1-1	П4 мойка кухонная	½"	550	ст. В: 1335 от Г	межос. 100
Т3-1	—"	½"	550	ст. В: 1435 от Г	межос. 100
К1-1	—"	Ø50	400	ст. В: 1385 от Г	
В1-2	П6** стиральная машина	½"	600	ст. В: 2115 от Б	кран машины
К1-2	—"	Ø40	600	ст. В: 2315 от Б	
В1-3	П1** ванна	½"	800	ст. А: 825 от Г	межос. 150
Т3-2	—"	½"	800	ст. А: 675 от Г	межос. 150
К1-3	—"	Ø50	50	ст. А: 200 от Г	
В1-4	П3** умывальник	½"	550	ст. В: 345 от Б	межос. 100
Т3-3	—"	½"	550	ст. В: 245 от Б	межос. 100
К1-4	—"	Ø50	500	ст. В: 295 от Б	
В1-5	П20 унитаз подвесной	½"	150	ст. Г: 240 от А	в раме инсталляции
К1-5	—"	Ø110	230	ст. Г: 390 от А	

* — высота по практике монтажа; сверить по паспорту прибора

Условные обозначения

- вывод В1 (код — в ведомости привязок)
- вывод Т3 (код — в ведомости привязок)
- вывод К1 (код — в ведомости привязок)
- сантехприбор по расстановке (габарит модели)
- чистовая поверхность стены (от неё привязки)
- стояк «Ст К1-N / Ст В1-N» (ГОСТ 21.601), Ø мм
- шахта / короб стояков, люк 300×400
- линия обрыва (граница фрагмента)
- А — обозначение стены А–Г (как на развёртках)

Допущения и предложения на листе

Основа листа: размеры сняты с плана заказчика, контрольный обмер не выполнен (К-5); высота потолка 2700 мм принята: на плане заказчика не указана (К-5); подрайон климата не задан — принят не северный (жилые от 2,5 м) (К-4); толщины стен приняты: наружные 250 мм, перегородки 120 мм — не обмерены (К-5); разрешённая мощность 15 кВт принята по типовой квартире, технических условий нет (К-6).

Знак «**» — предложение проектировщика, заказчиком не утверждено (согласовать с заказчиком): ИЗ-4: Т3; К-2: П1 — ванна 1500 вместо 1600 — не заходит в проход перед проёмом Д-4; перед ванной 680 мм — глубина помещения; П3 — умывальник у стены В справа от ванны — перед ним свободно 750 мм, до стены Б 90 мм; К-7: П6 — стиральная машина на кухне: в ванной и санузле места нет; подвод ХВС с шаровым краном, слив — встраиваемый сифон с обратным клапаном (водяной затвор), отдельная группа 6 щита с УЗО 30 мА.

Открытые вопросы и конфликты по листу: К-2, К-7.

См. лист открытых вопросов (лист 6, записи К-2, К-4–К-7; лист 7, запись ИЗ-4).

Примечания

1. Привязки выводов даны от чистовых поверхностей стен (облицовка на сторону: кухня-гостиная — 15 мм (по данным); ванная — 20 мм (по данным); санузел — 20 мм (по данным)); эти же грани — на развёртках и в раскладке плитки. Высоты — от чистого пола помещения.
2. Высоты и межосевые, отмеченные «*», приняты по практике монтажа; до черновой разводки сверить по паспорту выбранного прибора (смеситель, инсталляция, сифон).
3. Горячая вода (Т3**) — слева от холодной (В1), если смотреть на прибор. Допуск установки выводов: ±5 мм в группе, ±20 мм у отдельно стоящих.
4. Расчёт систем водоснабжения и канализации и подбор оборудования выполняет проектная организация; лист задаёт места и высоты выводов.
5. Стояки в коробах/шахтах Ш1 не замоноличивать; стояк К1 в коробе — звукоизоляция стояка в коробе без жёсткого контакта с трубой; к арматуре и ревизиям — люк не меньше 300×400.

1000 мм · печать 1:1

Изм.	Кол.уч	Лист	№ док.	Подп.	Дата
Разраб.		Кырлан А.С.			14.11.26
Пров.					
ГИП					
Н. контр.					
Утв.					

ГД-2026-006-АИ

Квартира 58 м²

Общая площадь 55,23* м² · * размеры приняты, не замерены (реестр — л. 6, 7, К-5)

Дизайн-проект интерьера

Стадия	Лист	Листов
РП	38	108

План выводов сантехники

М 1:25

Кырлан Александр Сергеевич


выпуск 14.11.2026 № bcee049e32 · стр. 43 из 128

Схема разводки водопровода и канализации


Схемы систем В1, Т3**, К1 · трассы принципиальные · уклоны в мм на 1 м · план М 1:200, фрагменты М 1:25

ПРЕДВАРИТЕЛЬНО · не для производства работ · открыто пунктов: 9 (реестр — л. 6, 7)


План квартиры (М 1:200)

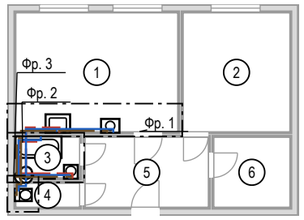


Фр. 1. Кухня-гостиная (М 1:25)

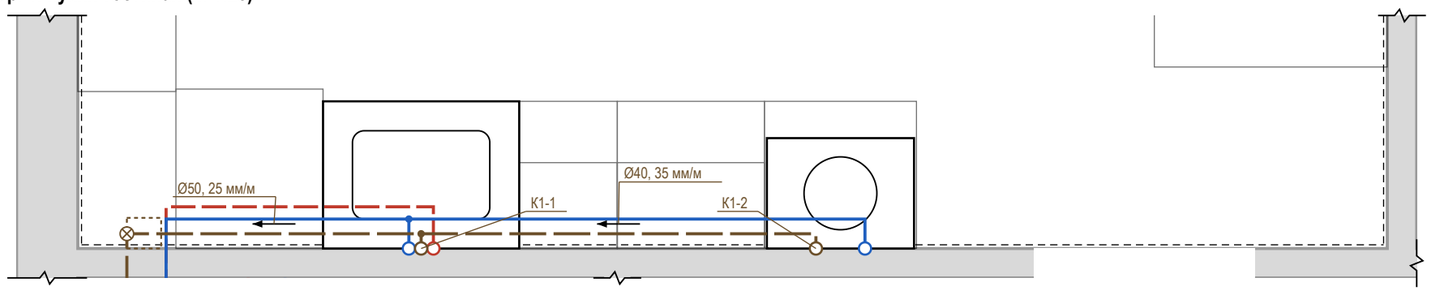

Фр. 2. Ванная (М 1:25)

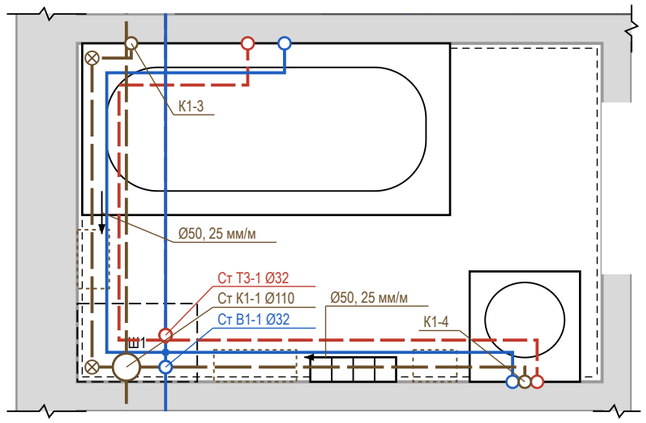

Фр. 3. Санузел (М 1:25)

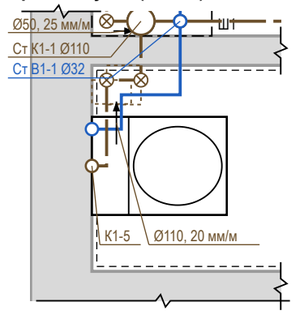

Условные обозначения

- В1 — водопровод хозяйственно-питьевой (ХВС), PP-R Ø20
- Т3 — горячее водоснабжение, подача (ГВС), PP-R Ø20
- К1 — канализация бытовая
- направление уклона К1 / пола: Ø, мм на 1 м
- ревизия (прочистка) К1 — доступ сохранить
- тройник (ответвление к прибору)
- короб К1 над чистым полом (ГКЛВ под плитку)
- вывод В1 (код — в ведомости привязок)
- вывод Т3 (код — в ведомости привязок)
- вывод К1 (код — в ведомости привязок)
- сантехприбор по расстановке (габарит модели)
- стояк «Ст К1-N / Ст В1-N» (ГОСТ 21.601), Ø мм
- шахта / короб стояков, люк 300×400
- линия обрыва (граница фрагмента)
- граница фрагмента на плане (Фр. N)

Профиль выпусков К1 (до врезки в стояк)

Выпуск	Прибор	Ø	L, м	i, мм/м	Δh, мм	Прокладка, мм
К1-5	П20 унитаз подвесной	Ø110	0,79	20	16	короб 160×140
К1-1	П4 мойка кухонная	Ø50	2,76	25	69	короб 150×110
К1-4	П3** умывальник	Ø50	1,69	25	42	короб 130×110
К1-3	П1** ванна	Ø50	1,62	25	41	короб 130×110
К1-2	П6** стиральная машина	Ø40	4,37	35	153	короб 230×110

Короб h×b: h — от чистого пола, b — от чистовой стены. Стяжка 90 мм — лист полов.

Узел ввода В1, Т3** (схема, без масштаба)



состав узла — по согласованию

⊗ Ст К1-1: ревизия на стояке — люк в коробе

Примечания

1. Трассы принципиальные, построены от стояков вдоль стен помещений; фактическое положение фиксируется исполнительной схемой с привязками (фото с рулеткой) до закрытия.
2. Уклон К1 не менее 1/d и не более 150 мм/м (СП 30.13330.2020, п. 19.1), приняты практические уклоны; поворот — двумя отводами 45°, ревизия после поворота, доступ сохранить. Стояк К1 в коробе — звукоизоляция стояка в коробе, без жёсткого контакта короба с трубой.
3. Решение по К1: стяжка 90 мм не укрывает трубы (нужно Ø + Δh + 45 мм) — выпуски идут над чистым полом вдоль стен; К1-5, К1-1, К1-4, К1-3, К1-2 — в коробе ГКЛВ под плитку (размеры в профиле). Короба — на развёртках; отметку низа врезки в стояк замерить до черновых работ.
4. Отводы К1-2 (4,4 м) длиннее 4 м без вентиляции — у прибора воздушный клапан Ø50 в доступном месте (за люком или в тумбе) либо вентилируемый отвод (EN 12056-2, табл. 4); предложение проектировщика, подбор — проектная организация.
5. Состав узла ввода В1, Т3** — по согласованию: на схеме типовой узел — кран шаровой, фильтр, счётчик, обратный клапан, кран; состав и места не определены (записи реестра нет). Доступ к арматуре — через люк не меньше 300×400. Водопровод — в штробе стен или в коробах; трубы испытать давлением до закрытия (акт скрытых работ).
6. Расчёт систем, диаметры магистралей и подбор оборудования выполняет проектная организация; врезка и перенос стояков — по согласованию с управляющей организацией. Арматуру и привязки сверить по паспортам приборов.
7. Ведомость выводов (код, прибор, высота, привязка) — лист 38; на схеме — только коды.

Допущения и предложения на листе. Знак «**» предложено (согласовать). См. лист открытых вопросов (листы 6, 7).

Изм.	Кол.уч	Лист	№ док.	Подп.	Дата
Разраб.		Кырлан А.С.			14.11.26
Пров.					
ГИП					
Н. контр.					
Утв.					

ГД-2026-006-АИ

Квартира 58 м²

Общая площадь 55,23* м² · * размеры приняты, не замерены (реестр — л. 6, 7, К-5)

Дизайн-проект интерьера

Стадия	Лист	Листов
РП	39	108

Схема разводки водопровода и канализации

М 1:200; 1:25

Кырлан Александр Сергеевич


выпуск 14.11.2026 № bcee049e32 · стр. 44 из 128

Аксонометрическая схема В1 (холодное водоснабжение)

аксонометрия · диаметры, уклоны, отметки, стояки и приборы · трассы принципиальные

ПРЕДВАРИТЕЛЬНО · не для производства работ · открыто пунктов: 9 (реестр — л. 6, 7)

Схема В1 (М 1:50)

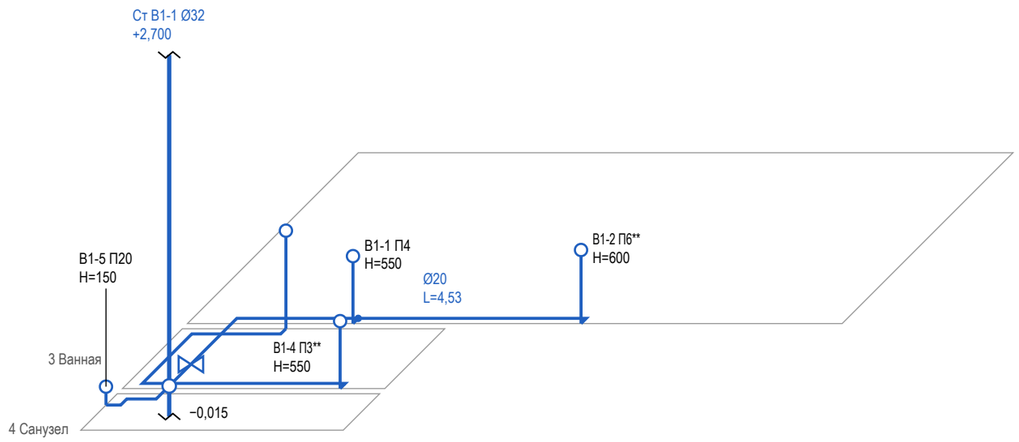

Ведомость выводов В1

Код	Прибор	H, мм	Ø, мм	Трасса, м
В1-2	П6** стиральная машина	600	20	4,53
В1-1	П4 мойка кухонная	550	20	0,12
В1-3	П1** ванна	800	20	2,23
В1-4	П3** умывальник	550	20	1,53
В1-5	П20 унитаз подвесной	150	20	0,80

Условные обозначения

- В1 — водопровод хозяйственно-питьевой (ХВС), PP-R Ø20
- вывод В1 (код — в ведомости привязок)
- стояк «Ст К1-N / Ст В1-N» (ГОСТ 21.601), Ø мм
- стояк в плане (на отметке пола); вертикаль — стояк по высоте, разрыв — перекрытие
- тройник (ответвление к прибору)
- кран шаровой

Примечания

1. Схема В1 построена по тем же трассам, что план разводки: положение в плане сохранено, глубина — в масштабе ×0,5. Трассы принципиальные; фактическое положение фиксируется исполнительной схемой до закрытия.
2. Высоты H — от чистого пола помещения, мм. Отметка прокладки магистрали В1 (в стяжке, в стене или по полу) в данных не задана: участки показаны на уровне пола условно (записи реестра нет).
3. Узел ввода В1 (кран, фильтр, счётчик, обратный клапан, кран) — на схеме разводки; состав узла ввода — по согласованию. Кран шаровой — на первом участке от стояка.
4. Трубы испытать давлением до закрытия (акт скрытых работ, опрессовка по СП 73.13330.2016).
5. Диаметры, высоты выводов и места кранов — по паспортам выбранных приборов и расчёту проектной организации.
6. Расчёт систем, диаметры магистралей и подбор оборудования выполняет проектная организация.

Допущения и предложения на листе. Знак «**» предложено (согласовать). См. лист открытых вопросов (листы 6, 7).

1000 мм · печать 1:1

Изм.	Кол.уч	Лист	№ док.	Подп.	Дата
Разраб.		Кырлан А.С.			14.11.26
Пров.					
ГИП					
Н. контр.					
Утв.					

ГД-2026-006-АИ

Квартира 58 м²

Общая площадь 55,23* м² · * размеры приняты, не замерены (реестр — л. 6, 7, К-5)

Дизайн-проект интерьера

Стадия	Лист	Листов
РП	40	108

Аксонометрическая схема В1 (холодное водоснабжение)

М 1:50

Кырлан Александр Сергеевич


выпуск 14.11.2026 № bcee049e32 · стр. 45 из 128

Аксонометрическая схема Т3 (горячее водоснабжение)

аксонометрия · диаметры, уклоны, отметки, стояки и приборы · трассы принципиальные

Схема Т3 (М 1:50)**

ПРЕДВАРИТЕЛЬНО · не для производства работ · открыто пунктов: 9 (реестр — л. 6, 7)

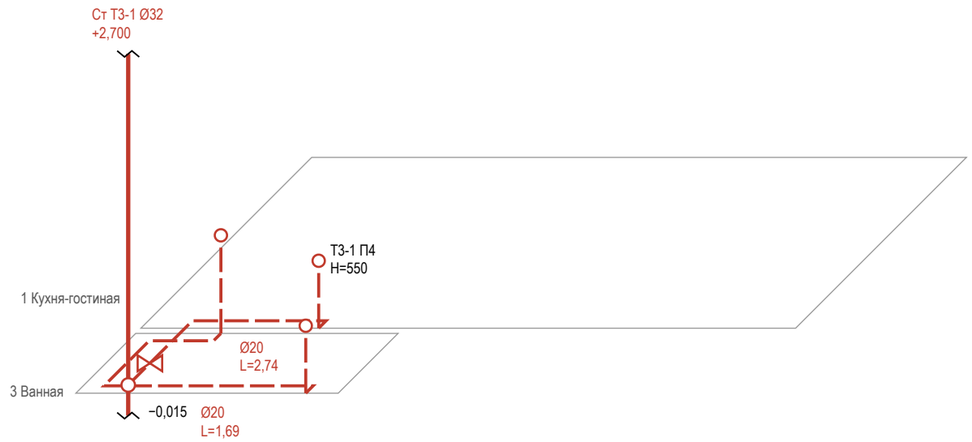

Ведомость выводов Т3**

Код	Прибор	H, мм	Ø, мм	Трасса, м
Т3-1	П4 мойка кухонная	550	20	2,74
Т3-2	П1** ванна	800	20	1,95
Т3-3	П3** умывальник	550	20	1,69

Условные обозначения

- Т3 — горячее водоснабжение, подача (ГВС), PP-R Ø20
- вывод Т3 (код — в ведомости привязок)
- стояк «Ст К1-N / Ст В1-N» (ГОСТ 21.601), Ø мм
- стояк в плане (на отметке пола); вертикаль — стояк по высоте, разрыв — перекрытие
- тройник (ответвление к прибору)
- кран шаровой

Примечания

1. Схема Т3** построена по тем же трассам, что план разводки: положение в плане сохранено, глубина — в масштабе ×0,5. Трассы принципиальные; фактическое положение фиксируется исполнительной схемой до закрытия.
2. Высоты H — от чистого пола помещения, мм. Отметка прокладки магистрали Т3** (в стяжке, в стене или по полу) в данных не задана: участки показаны на уровне пола условно (записи реестра нет).
3. Узел ввода Т3** (кран, фильтр, счётчик, обратный клапан, кран) — на схеме разводки; состав узла ввода — по согласованию. Кран шаровой — на первом участке от стояка.
4. Циркуляция ГВС в данных не задана — циркуляционного трубопровода на схеме нет (записи реестра нет).
5. Трубы испытать давлением до закрытия (акт скрытых работ, опрессовка по СП 73.13330.2016).
6. Диаметры, высоты выводов и места кранов — по паспортам выбранных приборов и расчёту проектной организации.
7. Расчёт систем, диаметры магистралей и подбор оборудования выполняет проектная организация.

1000 мм · печать 1:1

Допущения и предложения на листе. Знак «**» предложено (согласовать). См. лист открытых вопросов (листы 6, 7).

Изм.	Кол.уч	Лист	№ док.	Подп.	Дата
Разраб.		Кырлан А.С.			14.11.26
Пров.					
ГИП					
Н. контр.					
Утв.					

ГД-2026-006-АИ

Квартира 58 м²

Общая площадь 55,23* м² · * размеры приняты, не замерены (реестр — л. 6, 7, К-5)

Дизайн-проект интерьера

Стадия	Лист	Листов
РП	41	108

Аксонометрическая схема Т3 (горячее водоснабжение)

М 1:50

Кырлан Александр Сергеевич


выпуск 14.11.2026 № bcee049e32 · стр. 46 из 128

Аксонометрическая схема К1 (канализация)

аксонометрия · диаметры, уклоны, отметки, стояки и приборы · трассы принципиальные

Схема К1 (М 1:50)

ПРЕДВАРИТЕЛЬНО · не для производства работ · открыто пунктов: 9 (реестр — л. 6, 7)

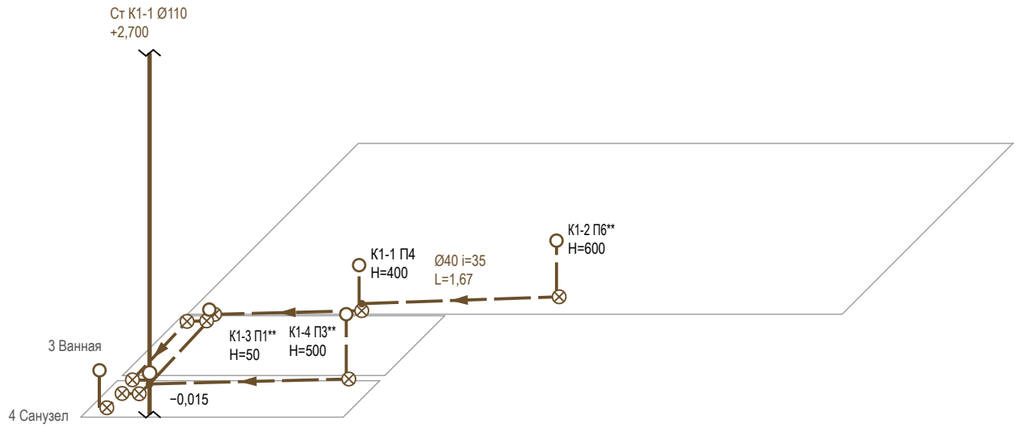

Ведомость выводов К1

Код	Прибор	Н, мм	Ø, i	Трасса, м
К1-5	П20 унитаз подвесной	230	110 i=20	0,79
К1-1	П4 мойка кухонная	400	50 i=25	2,76
К1-4	П3** умывальник	500	50 i=25	1,69
К1-3	П1** ванна	50	50 i=25	1,62
К1-2	П6** стиральная машина	600	40 i=35	1,67

Условные обозначения

- К1 — канализация бытовая
- вывод К1 (код — в ведомости привязок)
- стояк «Ст К1-N / Ст В1-N» (ГОСТ 21.601), Ø мм
- стояк в плане (на отметке пола); вертикаль — стояк по высоте, разрыв — перекрытие
- направление уклона К1 / пола: Ø, мм на 1 м
- ⊗ ревизия (прочистка) К1 — доступ сохранить
- • тройник (ответвление к прибору)

Примечания

1. Схема К1 построена по тем же трассам, что план разводки: положение в плане сохранено, глубина — в масштабе ×0,5. Трассы принципиальные; фактическое положение фиксируется исполнительной схемой до закрытия.
2. Отметки — от плиты перекрытия: низ трубы у врезки в стояк — отметка из данных выпуска, к прибору труба поднимается на уклон i, мм/м (уклон не менее 1/d и не более 150 мм/м, СП 30.13330.2020, п. 19.1); чистый пол — выше плиты на стяжку (высота пирога пола). Высота выпуска прибора Н — от чистого пола.
3. Ревизия — на повороте и в начале участка; стояк К1 в коробе с люком — звукоизоляция стояка в коробе; поворот — двумя отводами 45°.
4. Трубы испытать давлением до закрытия (акт скрытых работ, опрессовка по СП 73.13330.2016).
5. Диаметры, высоты выводов и места кранов — по паспортам выбранных приборов и расчёту проектной организации.
6. Расчёт систем, диаметры магистралей и подбор оборудования выполняет проектная организация.

Допущения и предложения на листе. Знак «**» предложено (согласовать). См. лист открытых вопросов (листы 6, 7).

1000 мм · печать 1:1

Изм.	Кол.уч	Лист	№ док.	Подп.	Дата
Разраб.		Кырлан А.С.			14.11.26
Пров.					
ГИП					
Н. контр.					
Утв.					

ГД-2026-006-АИ

Квартира 58 м²

Общая площадь 55,23* м² · * размеры приняты, не замерены (реестр — л. 6, 7, К-5)

Дизайн-проект интерьера

Стадия	Лист	Листов
РП	42	108

Аксонометрическая схема К1 (канализация)

М 1:50

Кырлан Александр Сергеевич


выпуск 14.11.2026 № bcee049e32 · стр. 47 из 128

Развёртки мокрых зон: выводы ВК. Кухня-гостиная

пом. 1 · выводы В1, Т3**, К1 на стенах · высоты от чистого пола, привязки от чистовых углов, мм

ПРЕДВАРИТЕЛЬНО · не для производства работ · открыто пунктов: 9 (реестр — л. 6, 7)

Стена В (М 1:20)

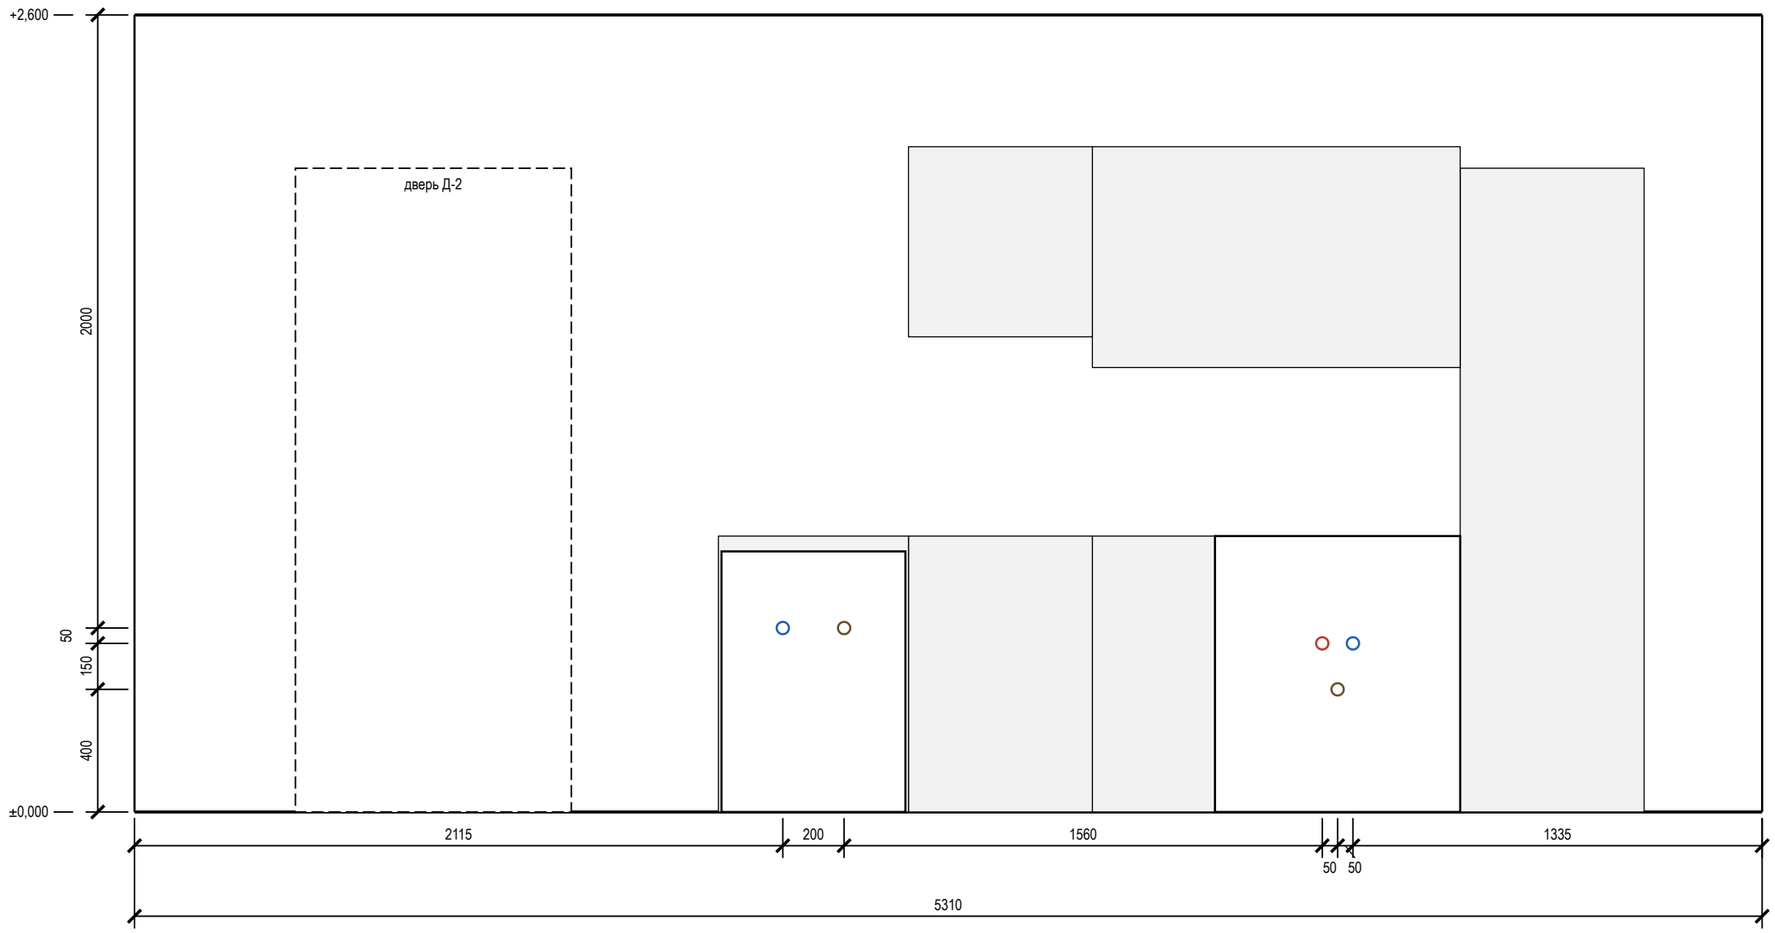

Ведомость привязок выводов (от чистого пола и угла)

Код	Прибор	Ø	Н, мм	Привязка, мм
В1-1	П4 мойка кухонная	½"	550	ст. В: 3975 от лев. угла
Т3-1	П4 мойка кухонная	½"	550	ст. В: 3875 от лев. угла
К1-1	П4 мойка кухонная	Ø50	400	ст. В: 3925 от лев. угла

Ведомость привязок (продолжение)

Код	Прибор	Ø	Н, мм	Привязка, мм
В1-2	П6** стиральная машина	½"	600	ст. В: 2115 от лев. угла
К1-2	П6** стиральная машина	Ø40	600	ст. В: 2315 от лев. угла

Условные обозначения

- вывод В1 (код — в ведомости привязок)
- вывод Т3 (код — в ведомости привязок)
- вывод К1 (код — в ведомости привязок)
- сантехприбор по расстановке (габарит модели)
- дверной проём; окно — сплошной контур

Допущения и предложения на листе

Основа листа: размеры сняты с плана заказчика, контрольный обмер не выполнен (К-5); высота потолка 2700 мм принята: на плане заказчика не указана (К-5); подрайон климата не задан — принят не северный (жилые от 2,5 м) (К-4); толщины стен приняты: наружные 250 мм, перегородки 120 мм — не обмерены (К-5); разрешённая мощность 15 кВт принята по типовой квартире, технических условий нет (К-6).

Знак «**» — предложение проектировщика, заказчиком не утверждено (согласовать с заказчиком): ИЗ-4: Т3; К-7: П6 — стиральная машина на кухне: в ванной и санузле места нет; подвод ХВС с шаровым краном, слив — встраиваемый сифон с обратным клапаном (водяной затвор), отдельная группа 6 щита с УЗО 30 мА.

См. лист открытых вопросов (лист 6, записи К-4–К-7; лист 7, запись ИЗ-4).

Примечания

1. Габариты и высоты приборов, межосевые смесителей и места кранов — по паспортам выбранных приборов, сверяются до разметки стен.
2. Высоты Н — от чистого пола помещения, мм; отметка чистого пола и потолка — у левого края вида (от ±0,000 объекта). Привязки — от левого чистового угла вида (облицовка стен вычтена), как на развёртках стен.
3. Ревизионные люки к арматуре и ревизиям в данных не заданы: место и размер не определены (записи реестра нет).
4. Мойка, ПММ и фильтр — выводы в шкафу мойки; диаметры и положение сифона и кранов сверить по паспортам приборов и чертежам модуля.
5. Часть подписей выводов не уместилась у знака: коды и высоты — в ведомости привязок.
6. Расчёт систем водоснабжения и канализации и подбор оборудования выполняет проектная организация; лист задаёт места и высоты выводов.

1000 мм · печать 1:1

Изм.	Кол.уч	Лист	№ док.	Подп.	Дата
Разраб.		Кырлан А.С.			14.11.26
Пров.					
ГИП					
Н. контр.					
Утв.					

ГД-2026-006-АИ

Квартира 58 м²

Общая площадь 55,23* м² · * размеры приняты, не замерены (реестр — л. 6, 7, К-5)

Дизайн-проект интерьера

Стадия	Лист	Листов
РП	43	108

Развёртки мокрых зон: выводы ВК. Кухня-гостиная

М 1:20

Кырлан Александр Сергеевич


выпуск 14.11.2026 № bcee049e32 · стр. 48 из 128

Развёртки мокрых зон: выводы ВК. Ванная


пом. 3 · выводы В1, Т3**, К1 на стенах · высоты от чистого пола, привязки от чистовых углов, мм

ПРЕДВАРИТЕЛЬНО · не для производства работ · открыто пунктов: 9 (реестр — л. 6, 7)


Стена А (М 1:25)

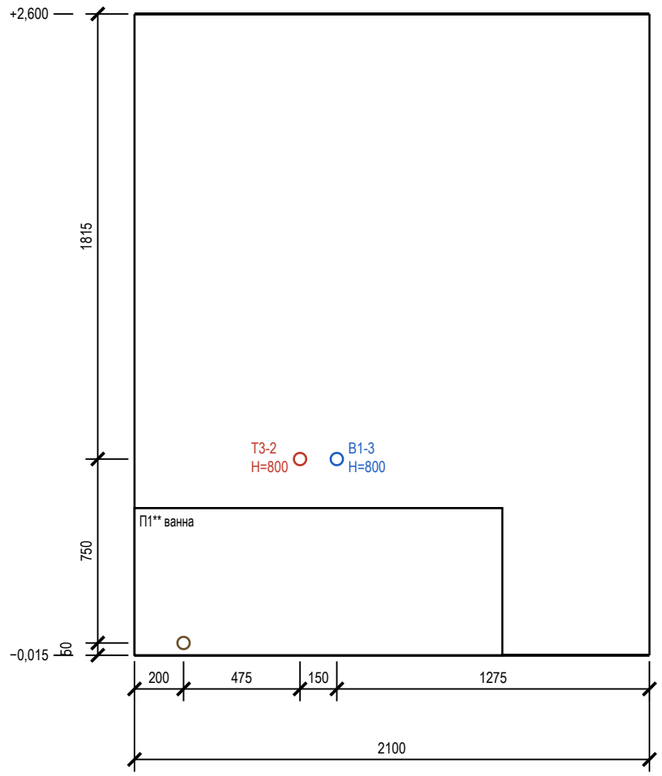


Стена Б (М 1:25)

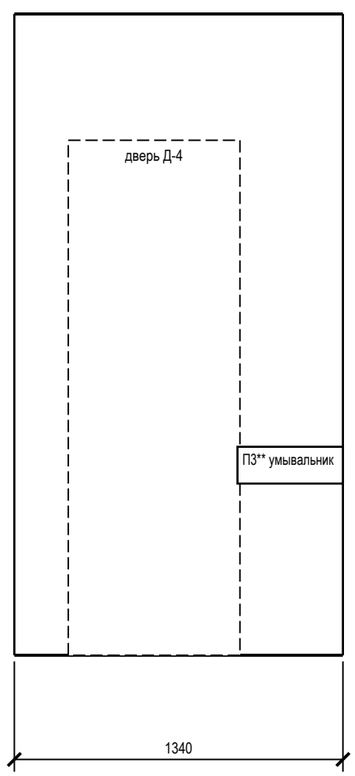

Стена В (М 1:25)

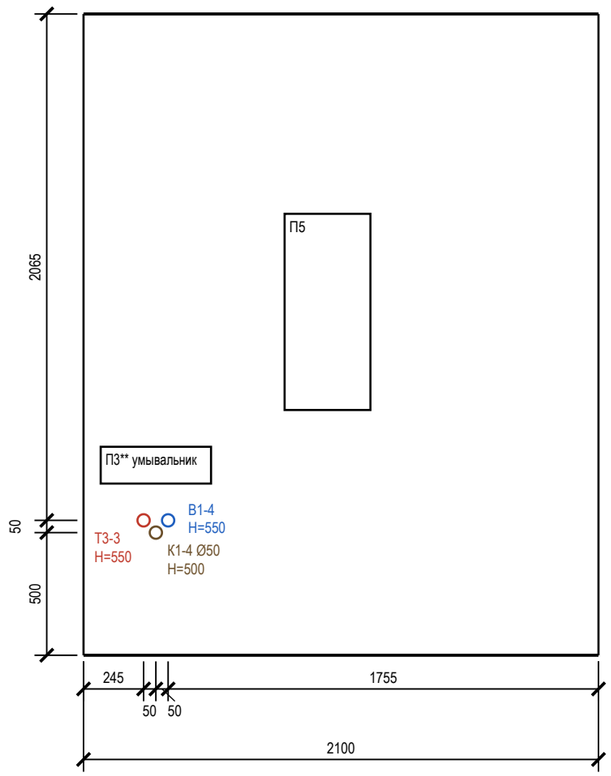

Стена Г (М 1:25)

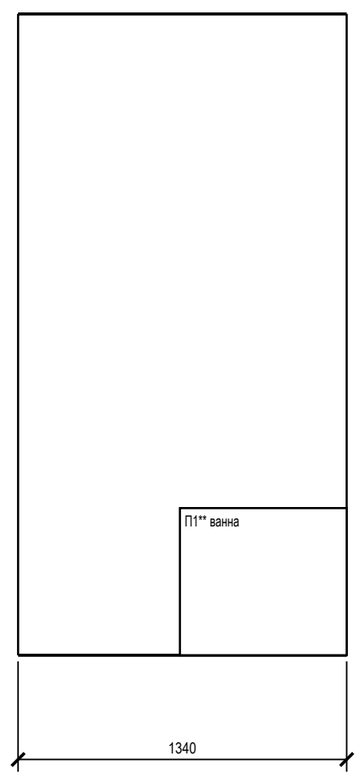

Ведомость привязок выводов (от чистого пола и угла)

Код	Прибор	Ø	H, мм	Привязка, мм
В1-3	П1** ванна	½"	800	ст. А: 825 от лев. угла
Т3-2	П1** ванна	½"	800	ст. А: 675 от лев. угла
К1-3	П1** ванна	Ø50	50	ст. А: 200 от лев. угла
В1-4	П3** умывальник	½"	550	ст. В: 345 от лев. угла
Т3-3	П3** умывальник	½"	550	ст. В: 245 от лев. угла
К1-4	П3** умывальник	Ø50	500	ст. В: 295 от лев. угла

Условные обозначения

- вывод В1 (код — в ведомости привязок)
- вывод Т3 (код — в ведомости привязок)
- вывод К1 (код — в ведомости привязок)
- сантехприбор по расстановке (габарит модели)
- дверной проём; окно — сплошной контур

Допущения и предложения на листе. Основа листа: размеры сняты с плана заказчика, контрольный обмер не выполнен (К-5); высота потолка 2700 мм принята: на плане заказчика не указана (К-5); подрайон климата не задан — принят не северный (жилые от 2,5 м) (К-4); толщины стен приняты: наружные 250 мм, перегородки 120 мм — не обмерены (К-5); разрешённая мощность 15 кВт принята по типовой квартире, технических условий нет (К-6). Знак «**» — предложение проектировщика, заказчиком не утверждено (согласовать с заказчиком): К-2: П1 — ванна 1500 вместо 1600 — не заходит в проход перед проёмом Д-4; перед ванной 680 мм — глубина помещения; П3 — умывальник у стены В справа от ванны — перед ним свободно 750 мм, до стены Б 90 мм. См. лист открытых вопросов (лист 6, записи К-2, К-4–К-6; лист 7, запись ИЗ-4).

Примечания

1. Габариты и высоты приборов, межосевые смесителей и места кранов — по паспортам выбранных приборов, сверяются до разметки стен.
2. Высоты Н — от чистого пола помещения, мм; отметка чистого пола и потолка — у левого края вида (от ±0,000 объекта). Привязки — от левого чистового угла вида (облицовка стен вычтена), как на развёртках стен.
3. Стояки в помещении: Ст К1-1 Ø110, Ст В1-1 Ø32, Ст Т3-1 Ø32 — положение на плане выводов; выводы подключаются к ним по схеме разводки.
4. Ревизионные люки к арматуре и ревизиям в данных не заданы: место и размер не определены (записи реестра нет).
5. Часть подписей выводов не уместилась у знака: коды и высоты — в ведомости привязок.
6. Расчёт систем водоснабжения и канализации и подбор оборудования выполняет проектная организация; лист задаёт места и высоты выводов.

1000 мм · печать 1:1

Изм.	Кол.уч	Лист	№ док.	Подп.	Дата
Разраб.		Кырлан А.С.			14.11.26
Пров.					
ГИП					
Н. контр.					
Утв.					

ГД-2026-006-АИ

Квартира 58 м²

Общая площадь 55,23* м² · * размеры приняты, не замерены (реестр — л. 6, 7, К-5)

Дизайн-проект интерьера

Стадия	Лист	Листов
РП	44	108

Развёртки мокрых зон: выводы ВК. Ванная

М 1:25

Кырлан Александр Сергеевич


выпуск 14.11.2026 № bcee049e32 · стр. 49 из 128

Развёртки мокрых зон: выводы ВК. Санузел

ПРЕДВАРИТЕЛЬНО · не для производства работ · открыто пунктов: 9 (реестр — л. 6, 7)

пом. 4 · выводы В1, Т3**, К1 на стенах · высоты от чистого пола, привязки от чистовых углов, мм

Стена Г (М 1:20)

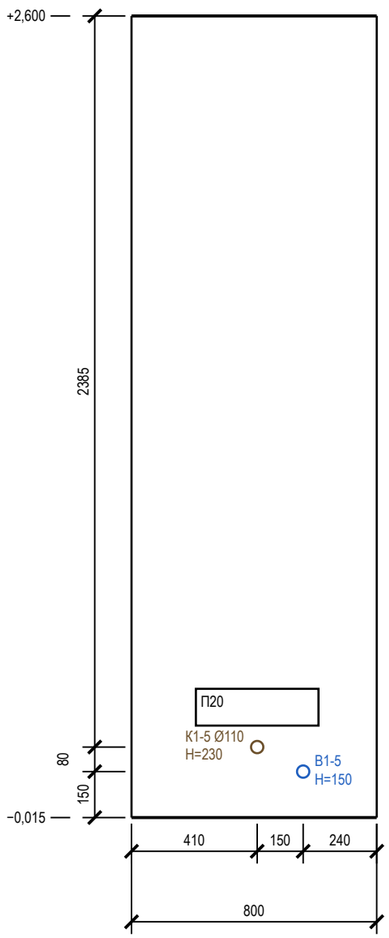

Ведомость привязок выводов (от чистого пола и угла)

Код	Прибор	Ø	H, мм	Привязка, мм
В1-5	П20 унитаз подвесной	½"	150	ст. Г: 560 от лев. угла
К1-5	П20 унитаз подвесной	Ø110	230	ст. Г: 410 от лев. угла

Условные обозначения

- вывод В1 (код — в ведомости привязок)
- вывод Т3 (код — в ведомости привязок)
- вывод К1 (код — в ведомости привязок)
- сантехприбор по расстановке (габарит модели)
- дверной проём; окно — сплошной контур

Примечания

1. Габариты и высоты приборов, межосевые смесителей и места кранов — по паспортам выбранных приборов, сверяются до разметки стен.
2. Высоты H — от чистого пола помещения, мм; отметка чистого пола и потолка — у левого края вида (от ±0,000 объекта). Привязки — от левого чистового угла вида (облицовка стен вычтена), как на развёртках стен.
3. Ревизионные люки к арматуре и ревизиям в данных не заданы: место и размер не определены (записи реестра нет).
4. Расчёт систем водоснабжения и канализации и подбор оборудования выполняет проектная организация; лист задаёт места и высоты выводов.

Допущения и предложения на листе

Основа листа: размеры сняты с плана заказчика, контрольный обмер не выполнен (К-5); высота потолка 2700 мм принята: на плане заказчика не указана (К-5); подрайон климата не задан — принят не северный (жилые от 2,5 м) (К-4); толщины стен приняты: наружные 250 мм, перегородки 120 мм — не обмерены (К-5); разрешённая мощность 15 кВт принята по типовой квартире, технических условий нет (К-6).

Знак «**» — предложение проектировщика, заказчиком не утверждено (согласовать с заказчиком): ИЗ-4: Т3.

См. лист открытых вопросов (лист 6, записи К-4–К-6; лист 7, запись ИЗ-4).

1000 мм · печать 1:1

Изм.	Кол.уч	Лист	№ док.	Подп.	Дата
Разраб.		Кырлан А.С.			14.11.26
Пров.					
ГИП					
Н. контр.					
Утв.					

ГД-2026-006-АИ

Квартира 58 м²

Общая площадь 55,23* м² · * размеры приняты, не замерены (реестр — л. 6, 7, К-5)

Дизайн-проект интерьера

Стадия	Лист	Листов
РП	45	108

Развёртки мокрых зон: выводы ВК. Санузел

М 1:20

Кырлан Александр Сергеевич

выпуск 14.11.2026 № bcee049e32 · стр. 50 из 128

Спецификация сантехнического оборудования

Форма 1 ГОСТ 21.110-2013 · ГД-2026-006-АИ-ВК.СО · приборы, арматура, трубопроводы

ПРЕДВАРИТЕЛЬНО · не для производства работ · открыто пунктов: 9 (реестр — л. 6, 7)

Поз.	Наименование и техническая характеристика	Тип, марка, обозначение документа	Код продукции	Поставщик	Ед. изм.	Кол.	Масса 1 ед., кг	Примечание
	Санитарные приборы							
1	Ванна встраиваемая акриловая 1500×700 мм, с каркасом, экраном и отверстием слив-перелив	акриловая 1500×700, смеситель настенный		выбор заказчика	шт	1		П1**
2	Унитаз подвесной безободковый, с сиденьем микролифт, крепёж и звукоизолирующая прокладка	Laufen Pro 8.2096.6.000.000.1		выбор заказчика	шт	1		П20
3	Инсталляция для подвесного унитаза: рама высотой 1120 мм, бачок, клавиша смыва (ось клавиши 1050 мм от чистого пола)	аналог		выбор заказчика	шт	1		П20; короб ГКЛВ
4	Умывальник подвесной 450×450 мм, с отверстием под смеситель и переливом	Laufen Pro S 8.1096.3.000.104.1		выбор заказчика	шт	1		П3**
5	Мойка кухонная 700×480 мм, с переливом	мойка врезная 700×480 в шкафу М5		с кухонной мебелью	шт	1		П4
6	Полотенцесушитель электрический, IP44, с терморегулятором	аналог		выбор заказчика	шт	1		П5
	Смесители, сифоны и арматура приборов							
7	Смеситель для ванны настенный однорычажный, межосевое 150 мм, с душевым набором (лейка, шланг, держатель)	аналог		выбор заказчика	шт	1		П1**
8	Смеситель для умывальника однорычажный, с донным клапаном	аналог		выбор заказчика	шт	1		П3**
9	Смеситель кухонный однорычажный, высокий излив	аналог		выбор заказчика	шт	1		П4
10	Обвязка ванны слив-перелив Ø40/50 с сифоном	аналог		выбор заказчика	шт	1		П1**
11	Сифон для умывальника бутылочный Ø32/40–50, с гофрой к выпуску	аналог		выбор заказчика	шт	1		П3**
12	Сифон для мойки Ø40/50	аналог		выбор заказчика	шт	1		П4
13	Сифон для стиральной машины встраиваемый в стену Ø50, с обратным клапаном	аналог		выбор заказчика	шт	1		П6**
14	Кран угловой ½"×½" с гибкой подводкой 40 см (умывальники, мойка)	аналог		выбор заказчика	шт	4		по 2 на прибор
15	Кран шаровой угловой ½"×¾" для подключения стиральной и посудомоечной машины	аналог		выбор заказчика	шт	1		П6**
	Трубопроводы							
16	Труба полипропиленовая PP-R PN20 Ø20×3,4 (В1)	ГОСТ 32415-2013		выбор заказчика	м	13,5	0,17	9,2 + 2,6 + 10 %
17	Труба PP-R, армированная стекловолокном, PN20 Ø20×2,8 (Т3**)	ГОСТ 32415-2013		выбор заказчика	м	9,5	0,15	6,4 + 1,9 + 10 %
18	Труба канализационная ПП Ø40 (К1)	ГОСТ 32414-2013		выбор заказчика	м	2,5		1,7 + 0,6 + 10 %
19	Труба канализационная ПП Ø50 (К1)	ГОСТ 32414-2013		выбор заказчика	м	8		6,1 + 0,9 + 10 %
20	Труба канализационная ПП Ø110 (К1)	ГОСТ 32414-2013		выбор заказчика	м	1,5		0,8 + 0,2 + 10 %
	Фасонные части и выводы							
21	Отвод канализационный ПП 45° Ø40	ГОСТ 32414-2013		выбор заказчика	шт	2		2 шт. на поворот
22	Отвод канализационный ПП 45° Ø50	ГОСТ 32414-2013		выбор заказчика	шт	12		2 шт. на поворот
23	Отвод канализационный ПП 45° Ø110	ГОСТ 32414-2013		выбор заказчика	шт	6		2 шт. на поворот
24	Тройник канализационный ПП 45° (врезки ветвей)	ГОСТ 32414-2013		выбор заказчика	шт	4		
25	Ревизия канализационная ПП (после поворота трассы)	ГОСТ 32414-2013		выбор заказчика	шт	5		доступ сохранить
26	Фитинги PP-R Ø20: тройники, угольники 90° (ветви и повороты В1, Т3**)	ГОСТ 32415-2013		выбор заказчика	шт	22		
27	Водорозетка PP-R Ø20×½" настенная, с креплением	ГОСТ 32415-2013		выбор заказчика	шт	8		коды — лист выводов
	Узлы ввода, люки, короба							
28	Кран шаровой латунный Ду15 PN16 (отключение ввода)	аналог		выбор заказчика	шт	2		Ст В1-1, Ст Т3-1
29	Фильтр сетчатый косой Ду15	аналог		выбор заказчика	шт	2		
30	Счётчик воды крыльчатый Ду15 (ХВ, ГВ), с поверкой	аналог		выбор заказчика	шт	2		пломба УК
31	Клапан обратный Ду15	аналог		выбор заказчика	шт	2		
32	Люк ревизионный нажимной под плитку 300×400 мм	аналог		выбор заказчика	шт	1		к стоякам и арматуре
33	Звукоизоляция стояка К1 в коробе: рулонный звукоизоляционный материал ≥ 10 мм, обмотка стояка на высоту этажа	аналог		выбор заказчика	м	2,7		Ст К1-1
34	Короб К1 над полом: профиль ПН/ПС, ГКЛВ 12,5 мм под плитку	аналог		выбор заказчика	м	1,6		сечение — лист разводки

Примечания

1. Форма 1 ГОСТ 21.110-2013, ширины граф изменены по п. 4.1. «Аналог» — аналог по характеристикам: модели внести до черновых работ, привязки выводов сверить по паспортам.
2. Бытовая техника не входит (показана арматура подключения), мойка — в комплекте кухни (марка — модуля кухни, как у столяра). Длины труб — трасса листа разводки + подъёмы + 10 %.
3. Стояк К1 в коробе — звукоизоляция стояка в коробе без жёсткого контакта короба с трубой.
4. Расчёт систем водоснабжения и канализации, диаметры магистралей и подбор оборудования выполняет проектная организация.

Допущения и предложения на листе

Основа листа: размеры сняты с плана заказчика, контрольный обмер не выполнен (К-5); высота потолка 2700 мм принята: на плане заказчика не указана (К-5); подрайон климата не задан — принят не северный (жилые от 2,5 м) (К-4); толщины стен приняты: наружные 250 мм, перегородки 120 мм — не обмерены (К-5); разрешённая мощность 15 кВт принята по типовой квартире, технических условий нет (К-6).

Знак «**» — предложение проектировщика, заказчиком не утверждено (согласовать с заказчиком): ИЗ-4: Т3; К-2: П1 — ванна 1500 вместо 1600 — не заходит в проход перед проёмом Д-4; перед ванной 680 мм — глубина помещения; П3 — умывальник у стены В справа от ванны — перед ним свободно 750 мм, до стены Б 90 мм; К-7: П6 — стиральная машина на кухне: в ванной и санузле места нет; подвод ХВС с шаровым краном, слив — встраиваемый сифон с обратным клапаном (водяной затвор), отдельная группа 6 щита с УЗО 30 мА.

См. лист открытых вопросов (лист 6, записи К-2, К-4–К-7; лист 7, запись ИЗ-4).

Изм.	Кол.уч	Лист	№ док.	Подп.	Дата	ГД-2026-006-АИ			
						Квартира 58 м²			
						Общая площадь 55,23* м² · * размеры приняты, не замерены (реестр — л. 6, 7, К-5)			
Разраб.		Кырлан А.С.			14.11.26	Дизайн-проект интерьера	Стадия	Лист	Листов
Пров.							РП	46	108
ГИП									
Н. контр.						Спецификация сантехнического оборудования	Кырлан Александр Сергеевич		
Утв.						М б/м			

выпуск 14.11.2026 № bcee049e32 · стр. 51 из 128

Техническое задание на подбор светильников

Параметры для подбора: светильники, ленты и блоки питания, слои света · б/м

Параметры светильников для подбора

Поз.	Марки	Наименование	Установка	Кол.	P, Вт	Σ P, Вт	Ф, лм	Тц, К	Ra	Угол, °	IP	Дим.	Слой	Группа	Пом.
1	Св1**	Подвесной	подвес, низ H=1450	1	40	40	3600	3000	90	—	20	—	общий	L1	1
2	Св2**	Трековая система	на потолке	4	12	48	950	3000	90	—	20	—	общий	L5	1
3	Св3	Линейный настенный	под верхними шкафами, H=1400	1	14	14	1080	3000	90	—	20	—	рабочий	L6	1
4	Св4	Потолочный накладной	на потолке	1	36	36	3200	2700	90	—	20	—	общий	L2	2
5	Св5**	Трековая система	на потолке	2	12	24	900	2700	90	—	20	—	общий	L2	2
6	Св6, Св7	Настенный (бра)	на стене, H=1300	2	4	8	250	2700	90	—	20	—	рабочий	L8	2
7	Св8	Встраиваемый точечный	в ГКЛ, корпус ≤ 70 мм	1	9	9	700	3000	90	—	44	—	общий	L4	3
8	Св9**	Настенный (бра)	над зеркалом, H=1900	1	6	6	400	3000	90	—	44	—	рабочий	L4	3
9	Св10	Встраиваемый точечный	в ГКЛ, корпус ≤ 70 мм	1	6	6	500	3000	90	—	44	—	общий	L9	4
10	Св11, Св12	Встраиваемый точечный	в ГКЛ, корпус ≤ 70 мм	2	9	18	800	3000	90	—	20	—	общий	L3	5
11	Св16	Потолочный накладной	на потолке, засветка стены	1	10	10	900	3000	90	—	20	—	общий	L7	6
		Итого		**17 шт**		**219**									

Слои света по помещениям

Пом.	Помещение	Слои света — группы включения (марки — в спецификации)	Σ P, Вт
1	Кухня-гостиная	общий — L1, L5; рабочий — L6	102
2	Спальня	общий — L2; рабочий — L8	68
3	Ванная	общий — L4; рабочий — L4	15
4	Санузел	общий — L9	6
5	Прихожая	общий — L3	18
6	Гардеробная	общий — L7	10

LED-ленты, линейные светильники и блоки питания

Марка	Пом.	L, м	U, В	Вт/м	Σ P, Вт	БП	P БП, Вт	Загр., %	Питание	Доступ к БП
Св2**	1	1,2	24	—	48	БП1	100	62	встроенный ввод	H=2300
—	1	1,8	24	—	14	БП1	100	62	встроенный ввод	H=2300
Св5**	2	0,8	24	—	24	БП2	60	40	встроенный ввод	H=2300

Слои света

общий — равномерный свет помещения, по норме освещённости

рабочий — местный свет задачи: столешница, зеркало, чтение у кровати

Допущения и предложения на листе

Основа листа: размеры сняты с плана заказчика, контрольный обмер не выполнен (К-5); высота потолка 2700 мм принята: на плане заказчика не указана (К-5); подрайон климата не задан — принят не северный (жилые от 2,5 м) (К-4); толщины стен приняты: наружные 250 мм, перегородки 120 мм — не обмерены (К-5); разрешённая мощность 15 кВт принята по типовой квартире, технических условий нет (К-6).

Знак «**» — предложение проектировщика, заказчиком не утверждено (согласовать с заказчиком): Св2 — общий свет зоны гостиной над журнальным столом М21 (трек шёл вдоль края стола М3 по проходу); трековая система 4 × 950 лм: поток принят до нормы освещённости, модель и паспорт не выбраны; Св5 — трековая система 2 × 900 лм: светильник добавлен проектировщиком, поток принят до нормы освещённости, модель и паспорт не выбраны; Св1 — подвес висел над проходом без заданной высоты, а стол — без света над ним: подвес по оси стола М3; Св9 — свет у зеркала — над зеркалом у умывальника по его оси (свет на лицо, а не над сантехникой).

См. лист открытых вопросов (лист 6, записи К-4–К-6).

Примечания

1. Позиции и марки Св — те же, что на плане освещения (лист 29) и в ведомости светильников (лист 31); группы L — по плану выключателей (лист 30).
2. Модели светильников не выбраны: лист — техническое задание на подбор. Модель по строке таблицы: поток, Тц, Ra, угол, IP и регулировка яркости не хуже указанных, мощность не больше; встраиваемые — под глубину короба (графа «Установка»). IP 20 — сухие помещения. После выбора моделей (артикул, производитель) лист выпускается как «Спецификация светильников».
3. Мощность и поток в таблице — требования к подбору (поток не меньше, мощность не больше указанных); после выбора модели — по её паспорту, Σ P — установленная мощность освещения. Оценка освещённости — на плане освещения; это не светотехнический расчёт.

Изм.	Кол.уч	Лист	№ док.	Подп.	Дата
Разраб.		Кырлан А.С.			14.11.26
Пров.					
ГИП					
Н. контр.					
Утв.					

ГД-2026-006-АИ

Квартира 58 м²

Общая площадь 55,23* м² · * размеры приняты, не замерены (реестр — л. 6, 7, К-5)

Дизайн-проект интерьера

Стадия	Лист	Листов
РП	47	108

Техническое задание на подбор светильников

М б/м

Кырлан Александр Сергеевич

выпуск 14.11.2026 № bcee049e32 · стр. 52 из 128

06

Потолки и ГКЛ-конструкции


Кырлан Александр Сергеевич

выпуск 14.11.2026 · bcee049e32 · стр. 53 из 128

План потолков

Уровни и марки потолков, короба с подсветкой, ниши под шторы, люки, вырезы · отметки низа от ±0,000 чистого пола · размеры в мм

Допущения и предложения на листе. Основа листа: размеры сняты с плана заказчика, контрольный обмер не выполнен (К-5); высота потолка 2700 мм принята: на плане заказчика не указана (К-5); подрайон климата не задан — принят не северный (жилые от 2,5 м) (К-4); толщины стен приняты: наружные 250 мм, перегородки 120 мм — не обмерены (К-5); разрешённая мощность 15 кВт принята по типовой квартире, технических условий нет (К-6). См. лист открытых вопросов (лист 6, записи К-4–К-6); по листу — К-4.

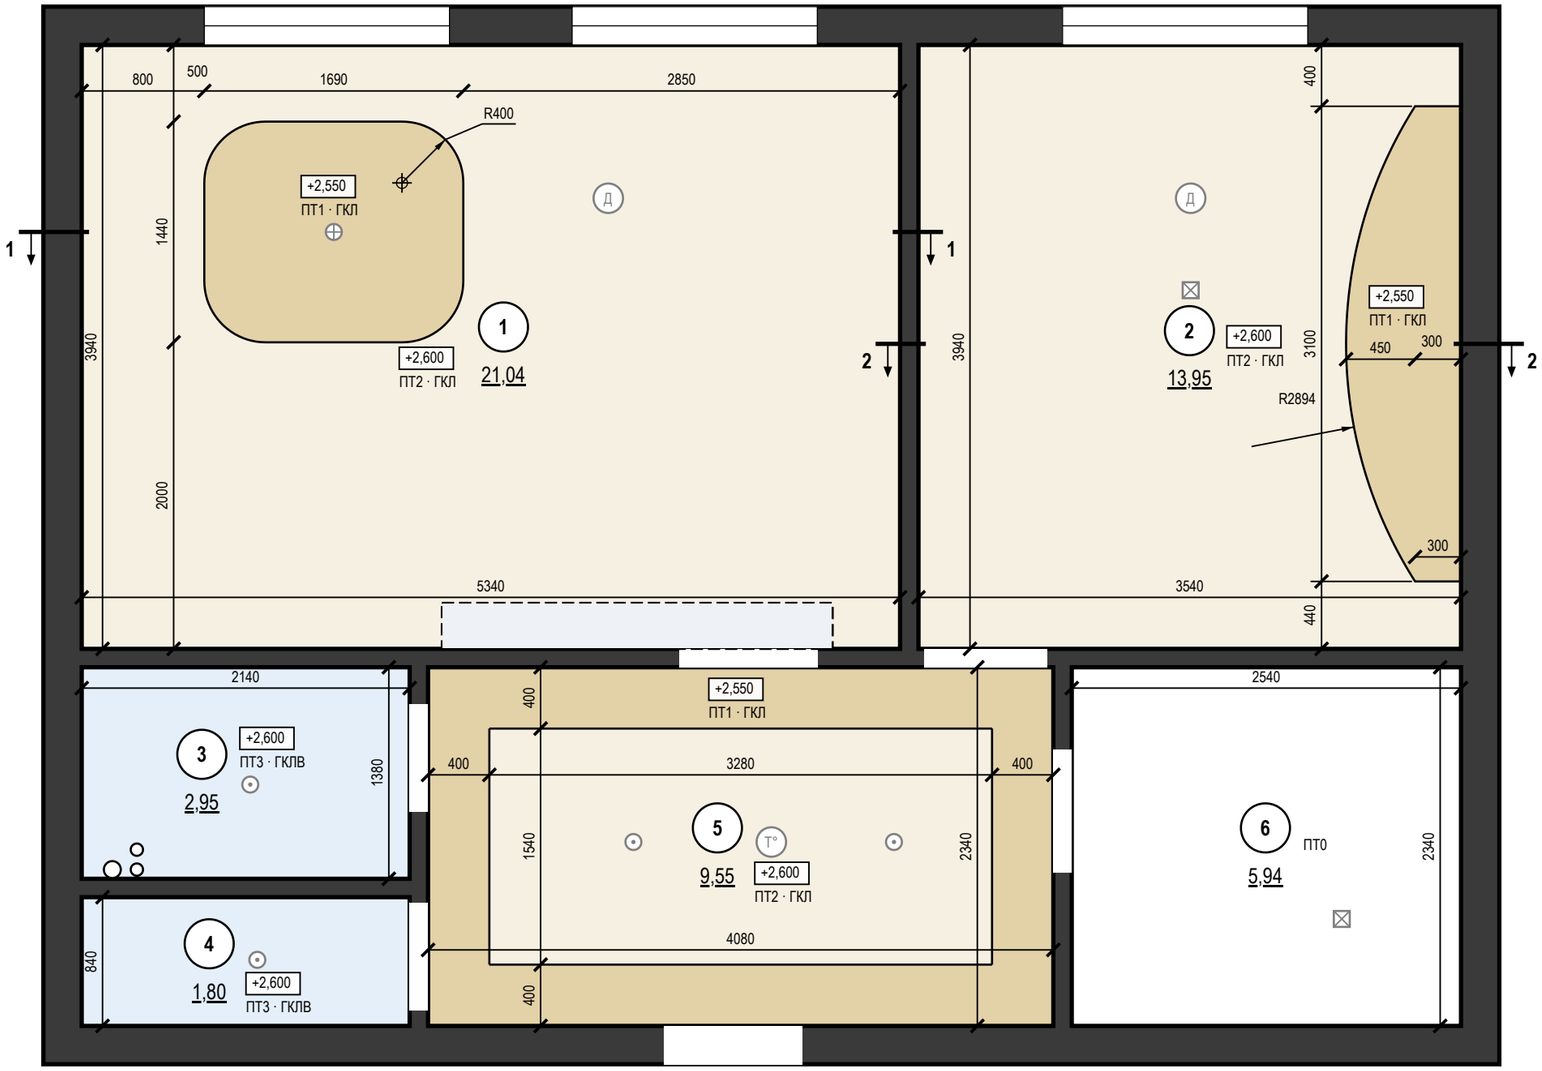

Ведомость потолков

Пом.	Марка	Конструкция	Низ / верх ниши	S, м²	Q
1	ПТ1	ГКЛ П113, остров	+2,550	2,30	Q3
1	ПТ2	ГКЛ П113	+2,600	18,74	Q3
2	ПТ1	ГКЛ П113, дуга	+2,550	1,88	Q3
2	ПТ2	ГКЛ П113	+2,600	12,07	Q3
3	ПТ3	ГКЛВ П113	+2,600	2,95	Q3
4	ПТ3	То же	+2,600	1,80	Q3
5	ПТ1	ГКЛ П113	+2,550	4,50	Q3
5	ПТ2	ГКЛ П113	+2,600	5,05	Q3
6	ПТ0	Существующий потолок, окраска	+2,700	5,94	
		Итого		**55,23**	

Ведомость вырезов и закладных в потолке

Марка	Устройство	Кол.	Пом.
	Светильник встраиваемый (марки — план освещения)	4	3, 4, 5
	Светильник накладной (марки — план освещения)	2	2, 6
	Светильник подвесной (марки — план освещения)	1	1
	Извещатель дымовой	2	1, 2
	Извещатель тепловой	1	5

Условные обозначения

- ПТ1 — ГКЛ по каркасу П113, низ +2,550
- ПТ2 — ГКЛ по каркасу П113, низ +2,600
- ПТ3 — ГКЛВ по каркасу П113, низ +2,600
- ПТ0 — существующий потолок, окраска, без подвесного потолка, низ +2,700
- граница уровней потолка (перепад)
- стояк: К1 — канализация, В1 — ХВС, Т3 — ГВС
- светильник подвесной — подложка с плана освещения
- светильник накладной — подложка с плана освещения
- светильник встраиваемый — подложка с плана освещения
- Д — извещатель дымовой на потолке — подложка
- T° — извещатель тепловой на потолке — подложка
- короб воздуховода вытяжки ГКЛ (трасса — план вентиляции)
- линия разреза у стен помещения, стрелка — направление взгляда
- +2,600 — отметка низа потолка, м (у ниши под шторы — верх ниши); под ней марка потолка
- 1 — номер помещения, площадь м²

Примечания

1. За отметку ±0,000 принят уровень чистого пола сухих помещений (готовое покрытие), а не существующего пола; пол пом. 3, 4 — −0,015; верх плиты перекрытия −0,064 — расчётный по пирогу пола, не замерен; существующий пол снимается до плиты, его отметка не замерена. Отметки в прямоугольниках — низ потолка; низ перекрытия +2,700. Марка потолка — одна конструкция и отметка на весь альбом.
2. Размеры помещений в свету (ширина × длина, мм), не поместившиеся на плане: пом. 4 — 2140 × 840.
3. Потолки ГКЛ — каркасная система П113: подвесы через 1000 (с запасом: СП 163, табл. 14 — до 1100 при 0,15 кН/м²), несущие профили через 500, основные через 1200 мм; листы — поперёк несущих профилей. В помещениях 3, 4 — ГКЛВ на оцинкованном каркасе.
4. Нижний уровень — пояс-короб по периметру шириной 400 мм, верхний — поле внутри пояса: пом. 5.
5. Примыкание к стенам: теневой шов 15 мм, техзазор 3 мм — пом. 1, 2, 5, по стенам, выровненным штукатуркой (узел 1); пом. 3, 4 — разделительная лента.
6. Светильники и потолочные устройства — подложка с планов освещения, слаботочных систем и вентиляции (положение — по ним); вырезы и закладные — по ведомости на листе, до обшивки; отверстия не совмещать с профилями, глубина корпуса светильника до 70 мм.
7. Разрезы 1–1, 2–2 — на листе 49; высоты мебели и дверных блоков сверены с низом потолка в разрезах; гибка бортов фигур и ленты ниш — там же; размеры фигурных уровней — фрагменты 1, 2 (лист 50).
8. Шпаклевание ГКЛ и условия приёмки — Q3: рассеянный дневной свет, осмотр с 2 м; боковой свет не оценивается.
9. Пом. 1: короб воздуховода кухонной вытяжки ГКЛ 300×200 мм (ширина от стены × высота), низ +2,500, длина 2,25 м — по трассе плана вентиляции, вдоль стен до входа в канал под воздуховод Ø125; каркас ПН 28×27 по стене и плите, ПП 60×27, лист ГКЛ 12,5.

1000 мм · печать 1:1

Изм.	Кол.уч	Лист	№ док.	Подп.	Дата
Разраб.		Кырлан А.С.			14.11.26
Пров.					
ГИП					
Н. контр.					
Утв.					

ГД-2026-006-АИ

Квартира 58 м²

Общая площадь 55,23* м² · * размеры приняты, не замерены (реестр — л. 6, 7, К-5)

Дизайн-проект интерьера

Стадия	Лист	Листов
РП	48	108

План потолков

М 1:40

Кырлан Александр Сергеевич


выпуск 14.11.2026 № bcee049e32 · стр. 54 из 128

Разрезы и узлы потолков

Разрезы по потолкам с отметками уровней · размеры в мм


Разрез 1–1 (М 1:40)

Пом. 1 Кухня-гостиная; линия разреза — план потолков, лист 48

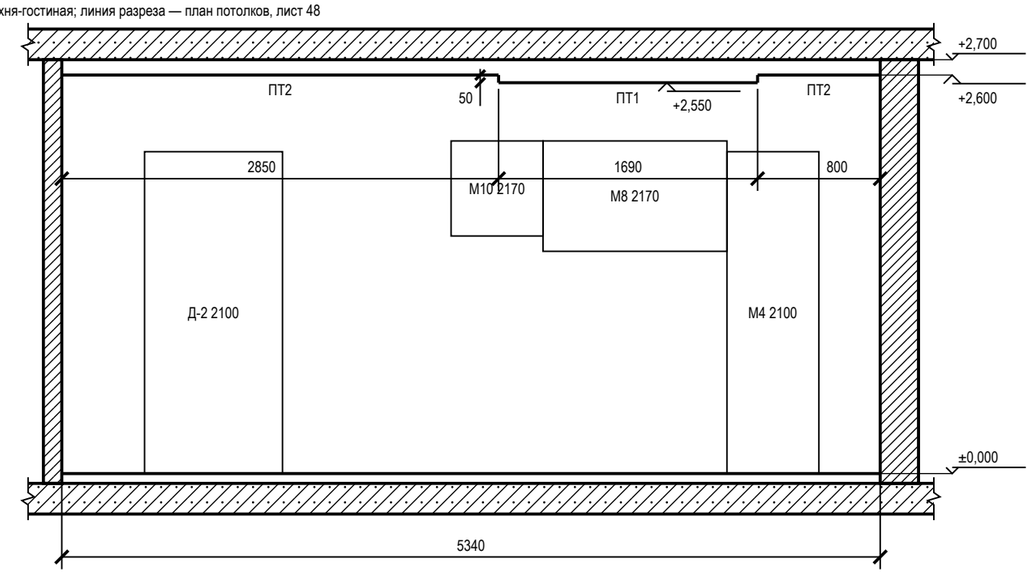

Разрез 2–2 (М 1:40)

Пом. 2 Спальня; линия разреза — план потолков, лист 48

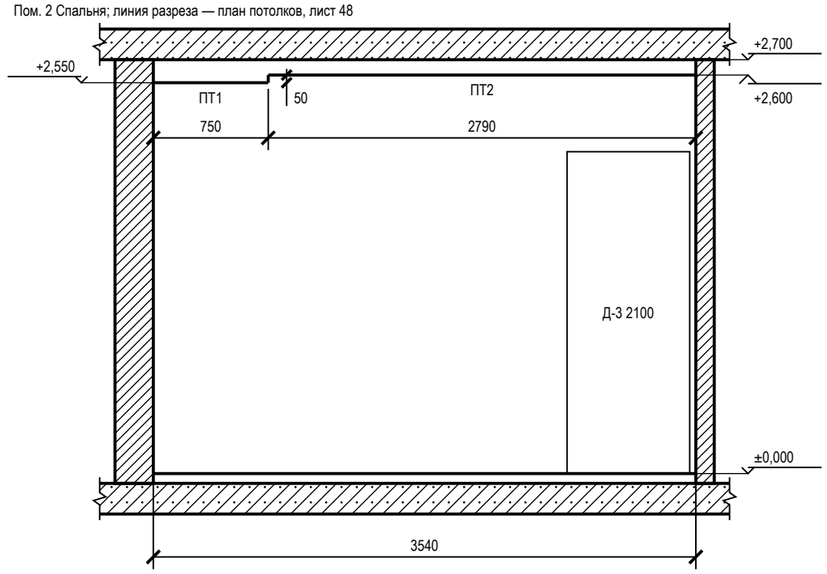

Условные обозначения

- плита перекрытия в сечении
- стена в сечении
- потолок ГКЛ в сечении; под линией — марка потолка (план потолков)
- мебель и дверные проёмы за секущей плоскостью; число — марка и верх от чистого пола, мм

Примечания

1. Разрезы — по линиям 1–1, 2–2 на плане потолков (лист 48). Отметки — от ±0,000 чистого пола, м; размеры — мм.
2. Высоты мебели и дверных блоков за секущей плоскостью сверены с низом потолка над ними: верх ниже низа короба и поля.
3. ГКЛ 12,5 мм по каркасу П113.
4. Толщины плит перекрытия и пирога пола показаны условно.
5. Ведомость объёмов потолков (лист ГКЛ, профиль, подвесы, лента, блоки питания, люки) — на листе 50.
6. Фрагменты 1, 2 — помещения с фигурными уровнями (размеры фигур, радиусы, отметки) — на листе 50.

1000 мм · печать 1:1

Допущения и предложения на листе

Основа листа: размеры сняты с плана заказчика, контрольный обмер не выполнен (К-5); высота потолка 2700 мм принята: на плане заказчика не указана (К-5); подрайон климата не задан — принят не северный (жилые от 2,5 м) (К-4); толщины стен приняты: наружные 250 мм, перегородки 120 мм — не обмерены (К-5); разрешённая мощность 15 кВт принята по типовой квартире, технических условий нет (К-6).
См. лист открытых вопросов (лист 6, записи К-4–К-6).

Изм.	Кол.уч	Лист	№ док.	Подп.	Дата
Разраб.		Кырлан А.С.			14.11.26
Пров.					
ГИП					
Н. контр.					
Утв.					

ГД-2026-006-АИ

Квартира 58 м²

Общая площадь 55,23* м² · * размеры приняты, не замерены (реестр — л. 6, 7, К-5)

Дизайн-проект интерьера

Стадия	Лист	Листов
РП	49	108

Разрезы и узлы потолков

М 1:40


Кырлан Александр Сергеевич

Разрезы и узлы потолков (продолжение)

Фрагменты фигурных уровней · ведомость объёмов · размеры в мм

Фрагмент 1. Пом. 1 Кухня-гостиная — уровни потолка (М 1:50)

Цепочки — от чистых граней стен; отметки — низ уровня от ±0,000

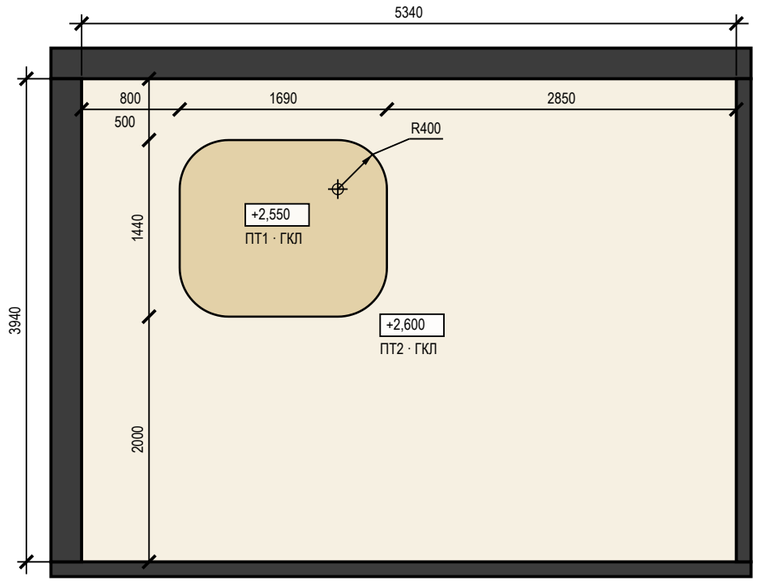


ПТ1 — низ +2,550

ПТ2 — низ +2,600

Фрагмент 2. Пом. 2 Спальня — уровни потолка (М 1:50)

Цепочки — от чистых граней стен; отметки — низ уровня от ±0,000

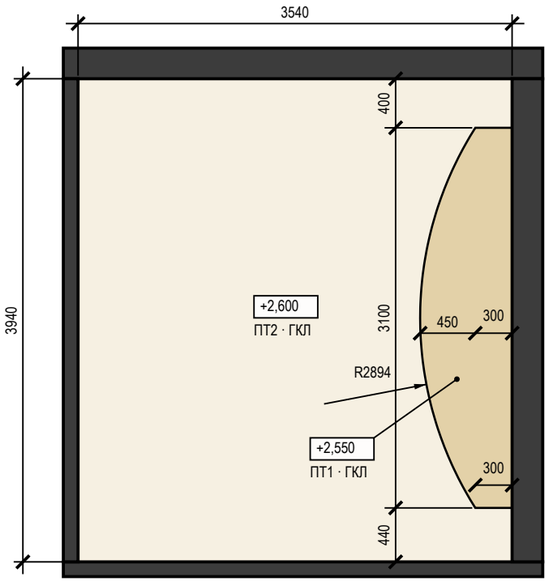

ПТ1 — низ +2,550

ПТ2 — низ +2,600

Ведомость объёмов потолков

Позиция	Ед.	Кол.	Пом.
Лист ГКЛ 12,5	м²	45,36	1, 2, 5
Лист ГКЛВ 12,5	м²	4,75	3, 4
Лист ГКЛ арочный 6,5	м²	0,25	1
Борта и карнизы (входят в площади листов выше)	м²	0,95	1, 2, 5
Профиль ПП 60×27	м	142,49	1, 2, 3, 4, 5
Профиль ПН 28×27	м	97,53	1, 2, 3, 4, 5
Подвес прямой	шт.	55	1, 2, 3, 4, 5
Анкер-клин к плите	шт.	55	1, 2, 3, 4, 5
Шуруп TN 3,5×25	шт.	1156	1, 2, 3, 4, 5
Лента армирующая для швов	м	60,29	1, 2, 3, 4, 5
Шпаклёвка для швов	кг	20,10	1, 2, 3, 4, 5
Грунтовка (швы)	л	5,02	1, 2, 3, 4, 5
Лента разделительная по периметру	м	59,36	1, 2, 3, 4, 5
Сплошная шпаклёвка и окраска (площадь развёртки)	м²	50,24	1, 2, 3, 4, 5

Допущения и предложения на листе

Основа листа: размеры сняты с плана заказчика, контрольный обмер не выполнен (К-5); высота потолка 2700 мм принята: на плане заказчика не указана (К-5); подрайон климата не задан — принят не северный (жилые от 2,5 м) (К-4); толщины стен приняты: наружные 250 мм, перегородки 120 мм — не обмерены (К-5); разрешённая мощность 15 кВт принята по типовой квартире, технических условий нет (К-6).

См. лист открытых вопросов (лист 6, записи К-4–К-6).

Примечания

1. ГКЛ 12,5 мм по каркасу П113; условные обозначения разрезов — на листе 49.
2. Фрагменты 1, 2 (план потолков — лист 48) — фигурные уровни потолка крупно: привязки краёв и центров фигур к чистым граням стен, радиусы (R) с центрами, хорда и стрелка дуги, отметки низа каждого уровня; цвета уровней — как на плане потолков.
3. Фигурные уровни: борт — ГКЛ по ПН с надрезами (на дуге шаг стоек борта 300 мм при R до 2500, 400 — до 5000) или по гнутому заводскому профилю (СП 163, 6.3.3); гибка: остров пом. 1 R400 — ГКЛ 6,5 мокрой гибкой; дуга пом. 2 R2894 — ГКЛ 12,5 сухой гибкой (СП 163, табл. 9).
4. Ведомость объёмов — по геометрии плана потолков: Лист ГКЛ 12,5 — плоскости уровней + борта (без арочных участков); Лист ГКЛВ 12,5 — плоскости уровней + борта; Лист ГКЛ арочный 6,5 — кривая борта × высота борта и стенки ниши × 2 слоя (R400 мокрая гибка); Борта и карнизы — длина перепада × перепад; Профиль ПП 60×27 — S × (1/шаг несущ. + 1/шаг осн.) + стойки бортов; Профиль ПН 28×27 — периметр стен + 2 × перепады + карнизы; Подвес прямой — по раскладке: S уровня / (шаг осн. × шаг подвесов), пояс уже шага — ряд вдоль пояса, фигура — по контуру; шаг подвесов — не больше табл. 14 СП 163; Анкер-клин к плите — по одному на подвес (Knauf П113); Шуруп TN 3,5×25 — 23 шт./м² (Knauf П113, табл. 2 альбома П 11); Лента армирующая для швов — 1,2 м/м² листа (Knauf); Шпаклёвка для швов — 0,4 кг/м² листа, только швы (Knauf); Грунтовка (швы) — 0,1 л/м² листа, только швы (Knauf); Лента разделительная по периметру — периметр стен под потолком ГКЛ; Сплошная шпаклёвка и окраска (площадь развёртки) — плоскости + борта; расход — по паспорту материала (норма расхода на сплошной слой не подтверждена); без запаса на подрезку (при закупке листа: ×1,075 при S > 20 м², ×1,175 — 10–20 м², ×1,275 — < 10 м²).

1000 мм · печать 1:1

Изм.	Кол.уч	Лист	№ док.	Подп.	Дата
Разраб.		Кырлан А.С.			14.11.26
Пров.					
ГИП					
Н. контр.					
Утв.					

ГД-2026-006-АИ

Квартира 58 м²

Общая площадь 55,23* м² · * размеры приняты, не замерены (реестр — л. 6, 7, К-5)

Дизайн-проект интерьера

Стадия	Лист	Листов
РП	50	108

Разрезы и узлы потолков (продолжение)

М 1:50

Кырлан Александр Сергеевич


выпуск 14.11.2026 № bcee049e32 · стр. 56 из 128

Раскладка плитки. Планы полов


Раскладка от чистовых размеров · размеры в мм · отметки от ±0,000

ПРЕДВАРИТЕЛЬНО · не для производства работ · открыто пунктов: 9 (реестр — л. 6, 7)

Фрагмент 1. Ванная (пом. 3). Пол 600×600, шов 2 мм (М 1:20)

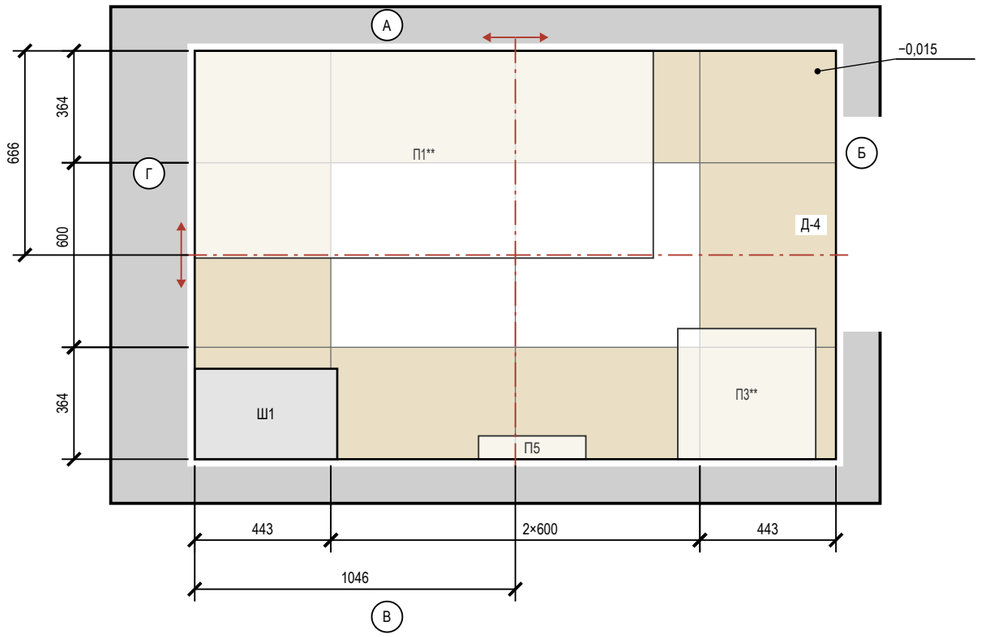

Фрагмент 2. Санузел (пом. 4). Пол 600×600, шов 2 мм (М 1:20)

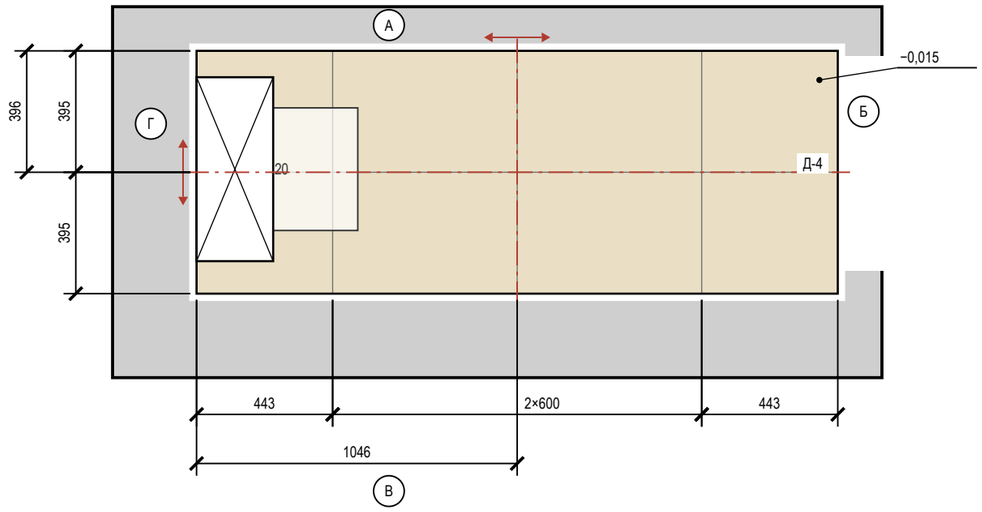

Ведомость материалов

Материал	Класс, код	Норма расхода	Кол-во
Затирка	класс не задан	(a+b)/ab·шов·t·1,6	3,9 кг
Клей	C2 S1	1,2 кг/м²·мм, слой 5	28 кг (2 меш.)
Клей	C2	1,2 кг/м²·мм, слой 5	266 кг (11 меш.)
Гидроизоляция	обмазочная, 2 слоя: пол, стены по периметру и зоны замачивания	по ТУ	13,4 м²
Демпф. лента	по периметру пола из плитки		21,0 м

Ведомость плитки

Помещение, поверхность	Плитка, код	Формат	Шов	S, м²	Целых	Подр.	С запасом
Ванная, пол	SG651622R	600×600	2	2,95	2	10	14
Ванная, стены А–Г	610015000370	1200×600	2	14,95	0	40	44
Ванная, короб стояков Ш1 489×319	610015000370	1200×600	2	1,99	0	10	12
Санузел, пол	SG651622R	600×600	2	1,80	0	8	9
Санузел, стены А–Г	610015000370	1200×600	2	13,40	0	30	34
Санузел, короб инсталляции	610015000370	1200×600	2	1,47	0	7	8
Прихожая, пол	SG651622R	600×600	2	9,55	10	18	31
Итого 600×600				14,30	12	36	54
Итого 600×1200				**31,80**	**0**	**87**	**98**

Условные обозначения

- плитка целая; тонкая линия — шов
- плитка с подрезкой (размер — на цепочке)
- ось старта; стрелки — направление укладки
- сантехприбор: габарит, высота по практике
- короб инсталляции: плитка пола — до короба
- короб стояков (Ш…): плитка пола — до короба
- отметка чистого пола на полке выноски, м
- (А) обозначение стены А–Г (как на развёртках)

Примечания

1. Раскладка от чистовых размеров: стены санузлов теряют 10 + 5 + 9 = 24 мм на сторону (штукатурка, клей, плитка); подрезки чистые, без шва.
2. Старт — от центра помещения (штрихпунктир, стрелки направление укладки); размер старта — от чистовых стен Г и А.
3. Раскладка пола «Прихожая» — на листе «Раскладка плитки. Прихожая».
4. Калибр партии не задан — до укладки замерить (рабочий размер W, ГОСТ 13996-2019) и пересчитать подрезки.
5. Количество: целые по раскладке + по одной на подрезку, запас 10 %; один артикул — одна партия и тон. Исключены поддон, короб, проёмы и места за коробом; S — по чистым граням: стены нетто = зона облицовки по ведомости отделки − место за коробом инсталляции 2,71 м² (плитку за коробом не кладут), короб отдельной строкой.
6. Клей C2 S1; C2 (ГОСТ Р 56387-2018), затирка класс не задан; расход — по ТУ выбранной марки.
7. Гидроизоляция: пол и стены 200 мм от ЧП; над ванной — до 2000 и 300 мм за борт (пом. 3) (см. развёртки); акт скрытых работ, пролив 24 ч.
8. Отметка чистого пола −0,015, порог 15 мм; стык с соседним покрытием — по оси полотна двери.

Допущения и предложения на листе

Основа листа: размеры сняты с плана заказчика, контрольный обмер не выполнен (К-5); высота потолка 2700 мм принята: на плане заказчика не указана (К-5); подрайон климата не задан — принят не северный (жилые от 2,5 м) (К-4); толщины стен приняты: наружные 250 мм, перегородки 120 мм — не обмерены (К-5); разрешённая мощность 15 кВт принята по типовой квартире, технических условий нет (К-6).

Знак «**» — предложение проектировщика, заказчиком не утверждено (согласовать с заказчиком): К-2: П1 — ванна 1500 вместо 1600 — не заходит в проход перед проёмом Д-4; перед ванной 680 мм — глубина помещения; П3 — умывальник у стены В справа от ванны — перед ним свободно 750 мм, до стены Б 90 мм.

См. лист открытых вопросов (лист 6, записи К-2, К-4–К-6).

1000 мм · печать 1:1

Изм.	Кол.уч	Лист	№ док.	Подп.	Дата
Разраб.		Кырлан А.С.			14.11.26
Пров.					
ГИП					
Н. контр.					
Утв.					

ГД-2026-006-АИ

Квартира 58 м²

Общая площадь 55,23* м² · * размеры приняты, не замерены (реестр — л. 6, 7, К-5)

Дизайн-проект интерьера

Стадия	Лист	Листов
РП	51	108

Раскладка плитки. Планы полов

М 1:20

Кырлан Александр Сергеевич


выпуск 14.11.2026 № bcee049e32 · стр. 57 из 128

Раскладка плитки. Прихожая

Раскладка от чистовых размеров · размеры в мм · высоты фартука от чистого пола

ПРЕДВАРИТЕЛЬНО · не для производства работ · открыто пунктов: 9 (реестр — л. 6, 7)

Фрагмент 1. Прихожая (пом. 5). Пол 600×600, шов 2 мм (М 1:20)

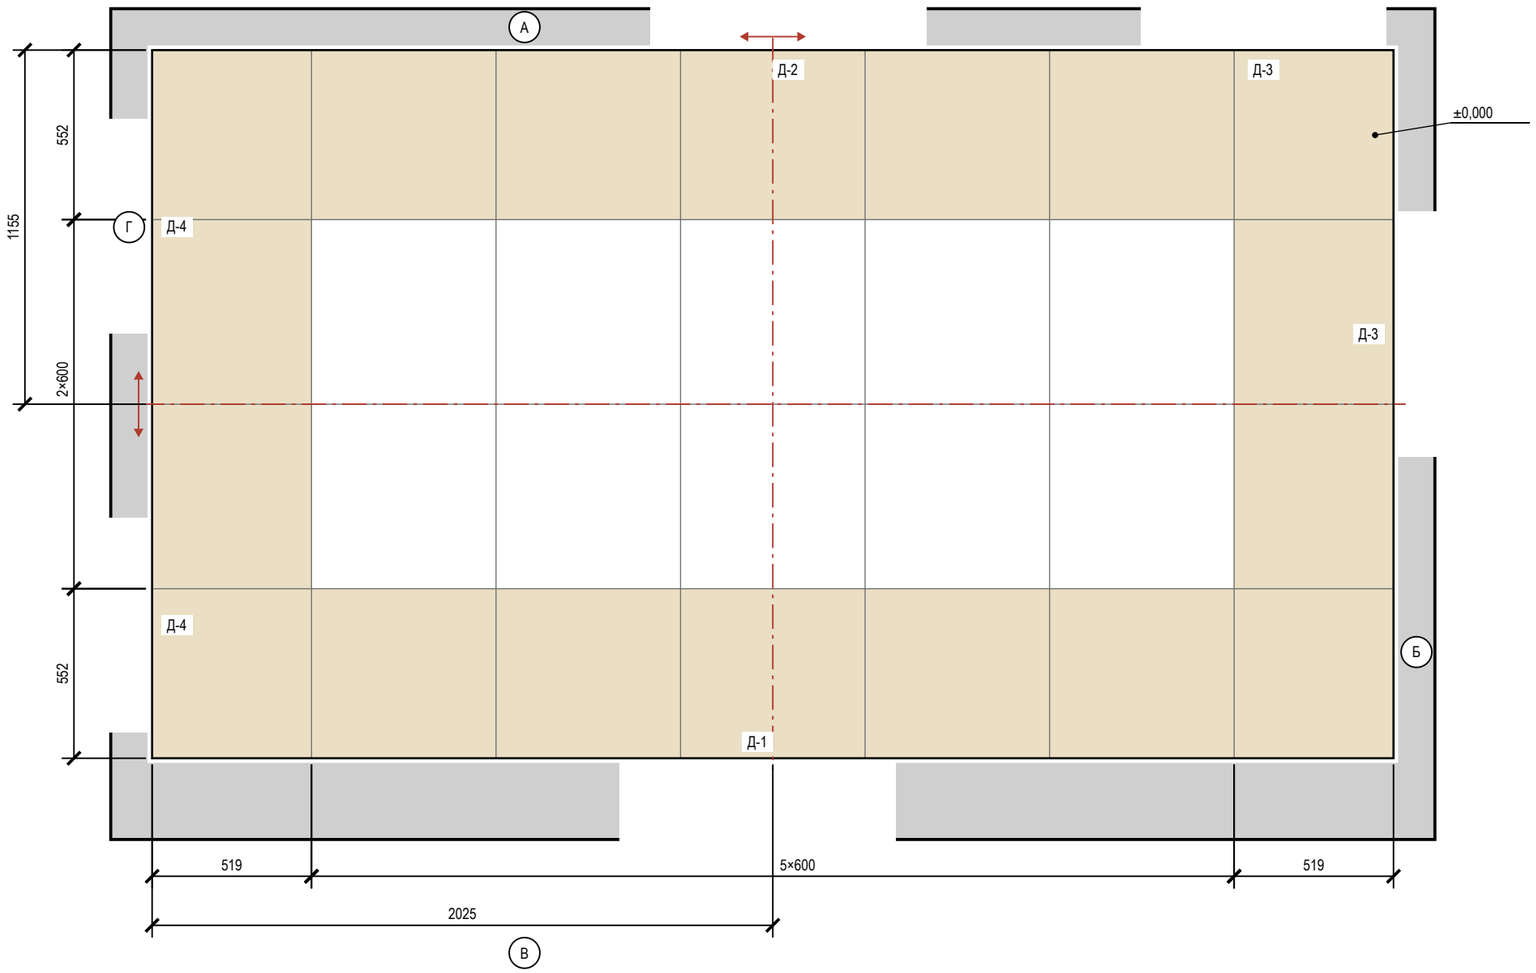

Условные обозначения

- плитка целая; тонкая линия — шов
- плитка с подрезкой (размер — на цепочке)
- ось старта; стрелки — направление укладки
- отметка чистого пола на полке выноски, м
- (А) обозначение стены А–Г (как на развёртках)

Подсчёт плитки

Поверхность	Формат	S, м²	Целых	Подр.	С запасом
Прихожая, пол	600×600	9,55	10	18	31

Примечания

1. Прихожая: керамогранит 600×600, длинная сторона — вдоль стен Б и Г, шов 2 мм, прямая раскладка от центра. Стены окрашены: раскладка от чистового контура минус штукатурка и шпаклёвка 15 мм на сторону (принято); подрезки 519 / 552 мм, срез — под плинтус.
2. Прихожая: деформационный зазор по периметру 8–10 мм под плинтусом; в проёмах — стык с соседним покрытием по оси полотна двери. Клей С2, затирка класс не задан.
3. Клей, затирка и итог по форматам — в ведомостях листа «Раскладка плитки. Планы полов».

Допущения и предложения на листе

Основа листа: размеры сняты с плана заказчика, контрольный обмер не выполнен (К-5); высота потолка 2700 мм принята: на плане заказчика не указана (К-5); подрайон климата не задан — принят не северный (жилые от 2,5 м) (К-4); толщины стен приняты: наружные 250 мм, перегородки 120 мм — не обмерены (К-5); разрешённая мощность 15 кВт принята по типовой квартире, технических условий нет (К-6).

См. лист открытых вопросов (лист 6, записи К-4–К-6).

1000 мм · печать 1:1

Изм.	Кол.уч	Лист	№ док.	Подп.	Дата
Разраб.		Кырлан А.С.			14.11.26
Пров.					
ГИП					
Н. контр.					
Утв.					

ГД-2026-006-АИ

Квартира 58 м²

Общая площадь 55,23* м² · * размеры приняты, не замерены (реестр — л. 6, 7, К-5)

Дизайн-проект интерьера

Стадия	Лист	Листов
РП	52	108

Раскладка плитки. Прихожая


М 1:20

Кырлан Александр Сергеевич

Раскладка плитки. Ванная. Развёртки стен

ПРЕДВАРИТЕЛЬНО · не для производства работ · открыто пунктов: 9 (реестр — л. 6, 7)

Пом. 3 · вид изнутри помещения · размеры в мм · высоты от чистого пола, отметки от ±0,000

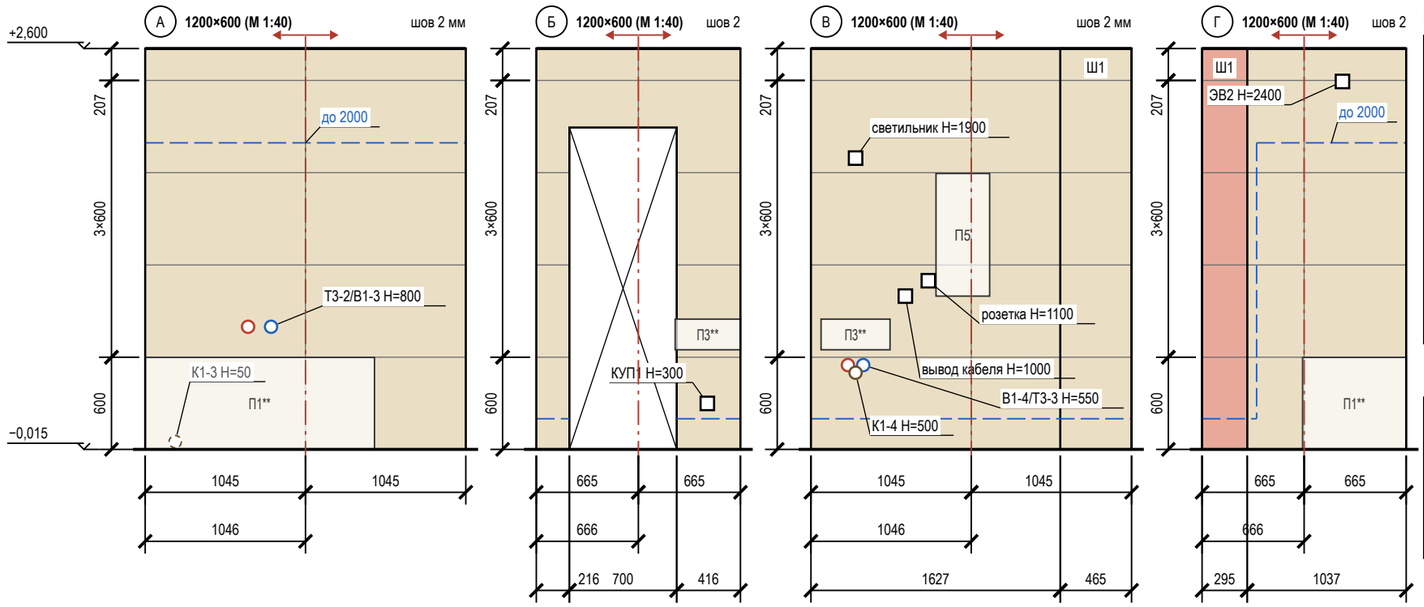

Подсчёт плитки по стенам и коробу

Поверхность	L × H, мм	S, м²	Целых	Подр.	С запасом	Подрезки: край / верх, мм
стена А	2092 × 2615	5,60	0	10	11	1045 / 1045; 207
стена Б	1332 × 2615	2,14	0	10	11	665 / 665; 207
стена В	2092 × 2615	4,38	0	10	11	1045 / 1045; 207
Ш1 489×319, ст. В	465 × 2615	1,22	0	5	6	лицо 465
стена Г	1332 × 2615	2,84	0	10	11	665 / 665; 207
Ш1 489×319, ст. Г	295 × 2615	0,77	0	5	6	лицо 295
Итого		**16,94**	**0**	**50**	**56**	

Сдвиг точек под раскладку

Точка (ВК, ЭОМ)	Стена	Проект: от угла / Н	Под раскладку: от угла / Н	Сдвиг, мм
розетка	В	766 / 1100	766 / 1203	Н +103
вывод кабеля	В	616 / 1000	616 / 902	Н −98
светильник	В	291 / 1900	291 / 1805	Н −95

Условные обозначения

- плитка целая; тонкая линия — шов
- плитка с подрезкой (размер — на цепочке)
- ось старта; стрелки — направление укладки
- верх гидроизоляции: 200 от ЧП, в мокрой зоне — «до …»
- проём — не облицовывается
- сантехприбор: габарит, высота по практике
- грань короба стояков (Ш…): своя сетка, за коробом плитку не кладут
- вывод В1 (код — в ведомости привязок)
- вывод Т3 (код — в ведомости привязок)
- вывод К1 (код — в ведомости привязок)
- вывод за прибором / в коробе (не на сетке)
- электроточка: марка и Н — по листам ЭОМ
- отметка уровня, м: ±0,000 — чистый пол жилых помещений
- низ потолка; серая полоса — стена без плитки
- (А) обозначение стены А–Г (как на развёртках)

Примечания

1. Вид изнутри, стены по часовой стрелке А → Г. Высоты — от чистого пола (−0,015), отметки — от ±0,000. Раскладка от чистовых размеров (штукатурка 10 + клей 5 + плитка 9 мм), подрезки чистые; старт — от оси стены, ряды от пола целыми.
2. Облицовка до потолка (+2,600).
3. Точки из таблицы сдвигов переносятся до черновой разводки (ЭОМ — по тем же числам).
4. Выводы ВК стоят по оси прибора и с прибором не двигаются — привязки по «Плану выводов сантехники» без сдвига; вне сетки (Т3-2/В1-3, В1-4/Т3-3, К1-4) отверстие в плитке коронкой по той же привязке, плитку не сдвигать.
5. Выводы — по «Плану выводов сантехники», электроточки — по ЭОМ, «*» — высота по практике; за приборами и в коробе (К1-3) — штриховым кольцом.
6. Гидроизоляция: 200 мм от ЧП по периметру; над ванной — до 2000 и 300 мм за борт (СП 29.13330.2011, п. 7.2 — на высоту замачивания); углы — лентой; акт скрытых работ, пролив.
7. Короб стояков Ш1: грани 465 мм (ст. В), 295 мм (ст. Г) — плиткой стен по рядам стены, целая плитка от наружного угла; угол — запил 45° или профиль; за коробом плитку не кладут. Люк 300×400 — на грани ст. В: высота — по месту ревизии стояка (положение стояков сверяется на объекте), кромки дверцы по швам сетки, дверца нажимная под плитку.

Допущения и предложения на листе

Основа листа: размеры сняты с плана заказчика, контрольный обмер не выполнен (К-5); высота потолка 2700 мм принята: на плане заказчика не указана (К-5); подрайон климата не задан — принят не северный (жилые от 2,5 м) (К-4); толщины стен приняты: наружные 250 мм, перегородки 120 мм — не обмерены (К-5); разрешённая мощность 15 кВт принята по типовой квартире, технических условий нет (К-6).

Знак «**» — предложение проектировщика, заказчиком не утверждено (согласовать с заказчиком): К-2: П1 — ванна 1500 вместо 1600 — не заходит в проход перед проёмом Д-4; перед ванной 680 мм — глубина помещения; П3 — умывальник у стены В справа от ванны — перед ним свободно 750 мм, до стены Б 90 мм.

См. лист открытых вопросов (лист 6, записи К-2, К-4–К-6).

1000 мм · печать 1:1

Изм.	Кол.уч	Лист	№ док.	Подп.	Дата
Разраб.		Кырлан А.С.			14.11.26
Пров.					
ГИП					
Н. контр.					
Утв.					

ГД-2026-006-АИ

Квартира 58 м²

Общая площадь 55,23* м² · * размеры приняты, не замерены (реестр — л. 6, 7, К-5)

Дизайн-проект интерьера

Стадия	Лист	Листов
РП	53	108

Раскладка плитки. Ванная. Развёртки стен

М 1:40


Кырлан Александр Сергеевич

выпуск 14.11.2026 № bcee049e32 · стр. 59 из 128

Раскладка плитки. Санузел. Развёртки стен

ПРЕДВАРИТЕЛЬНО · не для производства работ · открыто пунктов: 9 (реестр — л. 6, 7)

Пом. 4 · вид изнутри помещения · размеры в мм · высоты от чистого пола, отметки от ±0,000

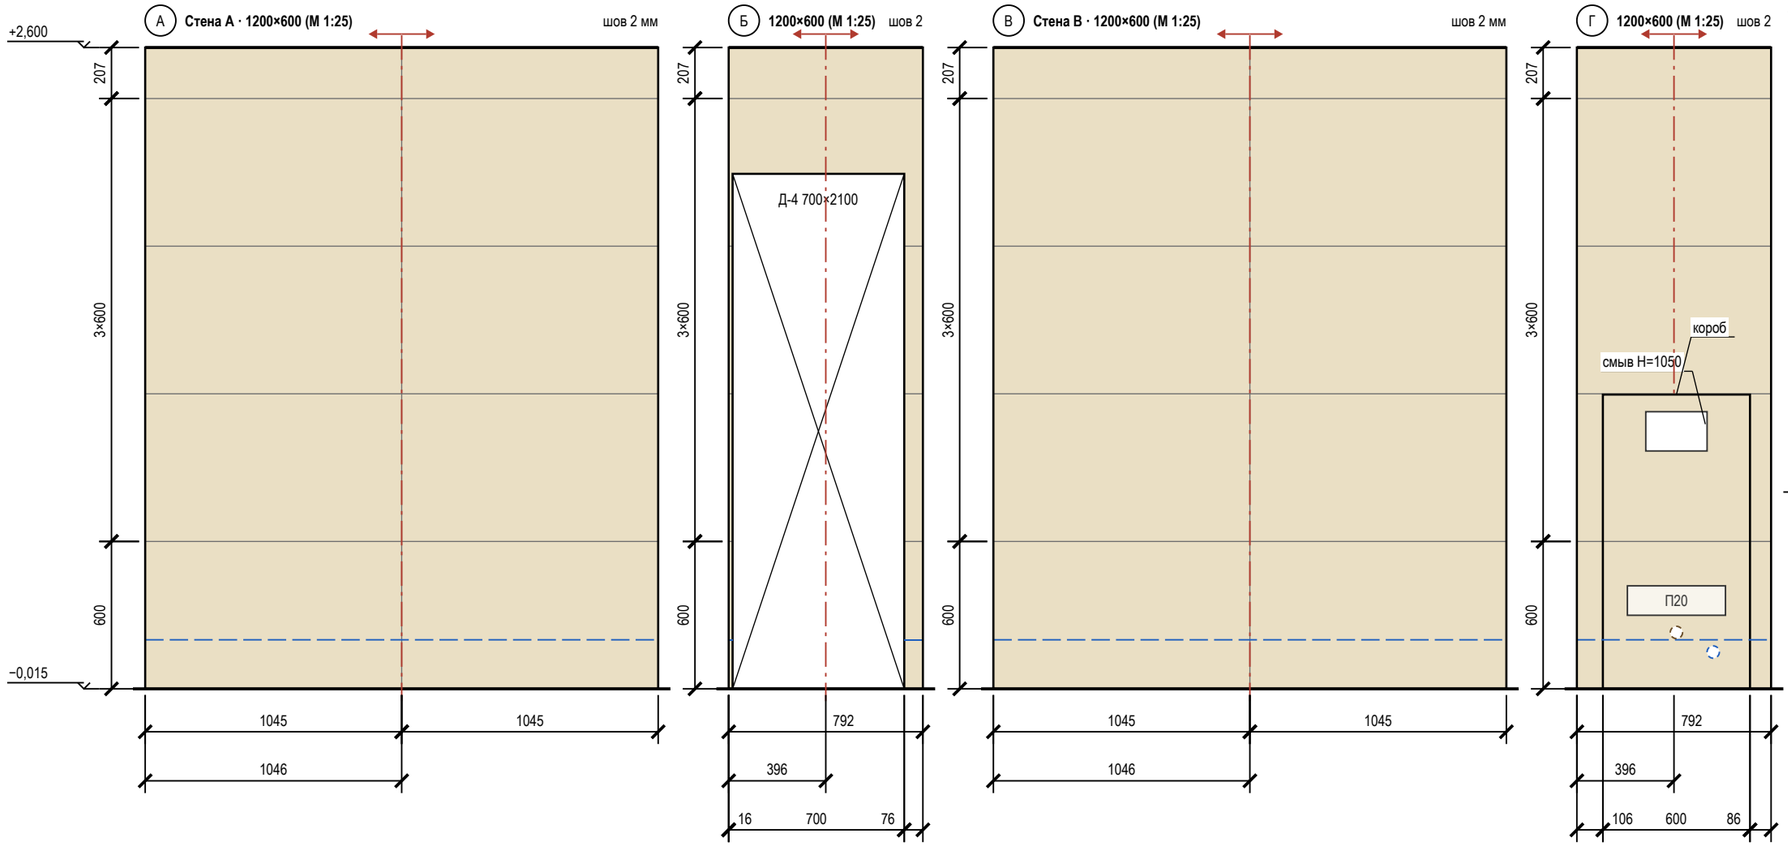

Условные обозначения

- плитка целая; тонкая линия — шов
- плитка с подрезкой (размер — на цепочке)
- ось старта; стрелки — направление укладки
- верх гидроизоляции: 200 от ЧП, в мокрой зоне — «до …»
- проём — не облицовывается
- сантехприбор: габарит, высота по практике
- короб инсталляции, в нём кнопка смыва 250×160
- вывод В1 (код — в ведомости привязок)
- вывод К1 (код — в ведомости привязок)
- вывод за прибором / в коробе (не на сетке)
- отметка уровня, м: ±0,000 — чистый пол жилых помещений
- низ потолка; серая полоса — стена без плитки
- А — обозначение стены А–Г (как на развёртках)

Подсчёт плитки по стенам и коробу

Поверхность	L × H, мм	S, м²	Целых	Подр.	С запасом	Подрезки: край / верх, мм
стена А	2092 × 2615	5,60	0	10	11	1045 / 1045; 207
стена Б	792 × 2615	0,73	0	5	6	792; 207
стена В	2092 × 2615	5,60	0	10	11	1045 / 1045; 207
стена Г	792 × 2615	1,48	0	5	6	792; 207
короб (ст. Г)	600×1200×250	1,47	0	7	8	лицо 600; бок. 250
Итого		**14,87**	**0**	**37**	**42**	

Примечания

1. Вид изнутри, стены по часовой стрелке А → Г. Высоты — от чистого пола (−0,015), отметки — от ±0,000. Раскладка от чистовых размеров (штукатурка 10 + клей 5 + плитка 9 мм), подрезки чистые; старт — от оси стены, ряды от пола целыми.
2. Облицовка до потолка (+2,600).
3. Открытые выводы и электроточки — на шве или в центре плитки (допуск 10 мм; плитка от 900 мм по высоте — на шве или не ближе 60 мм к нему).
4. Выводы — по «Плану выводов сантехники», электроточки — по ЭОМ, «*» — высота по практике; за приборами и в коробе (В1-5, К1-5) — штриховым кольцом.
5. Гидроизоляция: 200 мм от ЧП по периметру; углы — лентой; акт скрытых работ, пролив.
6. Короб 600×1200×250: лицо 600 мм от оси кнопки смыва, боковины, полка; углы — запил 45° или профиль; за коробом плитку не кладут.
7. Между коробом и углом полоса 86 и 106 мм — довести короб до угла.

Допущения и предложения на листе

Основа листа: размеры сняты с плана заказчика, контрольный обмер не выполнен (К-5); высота потолка 2700 мм принята: на плане заказчика не указана (К-5); подрайон климата не задан — принят не северный (жилые от 2,5 м) (К-4); толщины стен приняты: наружные 250 мм, перегородки 120 мм — не обмерены (К-5); разрешённая мощность 15 кВт принята по типовой квартире, технических условий нет (К-6).

См. лист открытых вопросов (лист 6, записи К-4–К-6).

1000 мм · печать 1:1

Изм.	Кол.уч	Лист	№ док.	Подп.	Дата
Разраб.		Кырлан А.С.			14.11.26
Пров.					
ГИП					
Н. контр.					
Утв.					

ГД-2026-006-АИ

Квартира 58 м²

Общая площадь 55,23* м² · * размеры приняты, не замерены (реестр — л. 6, 7, К-5)

Дизайн-проект интерьера	Стадия	Лист	Листов
	РП	54	108

Раскладка плитки. Санузел. Развёртки стен

М 1:25

Кырлан Александр Сергеевич

выпуск 14.11.2026 № bcee049e32 · стр. 60 из 128

07

Полы и отделка

Кырлан Александр Сергеевич

выпуск 14.11.2026 · bcee049e32 · стр. 61 из 128

План полов


Покрытия, направление укладки, отметки чистого пола, стыки · размеры в мм · отметки в м

Условные обозначения

- тип 1 — инженерная доска, линии — вдоль доски
- тип 2 — керамогранит 600×600, сетка — формат плитки
- тип 3 — керамогранит 600×600, сетка — формат плитки
- номер типа пола (экспликация полов)
- схема пола, без масштаба: плита — штриховка, стяжка — точки, звукоизоляция — зигзаг, гидроизоляция — утолщённая линия с заведением на стену
- направление укладки (длинная сторона доски)
- отметка чистого пола, м
- стык в проёме: решение не задано
- стык в проёме: порог
- СТ1 — марка стыка (ведомость стыков)
- стояк: К1 — канализация, В1 ХВС, Т3 — ГВС
- 1 — номер помещения, площадь м²

Отметки по высоте

±0,000	чистый пол пом. 1, 2, 5, 6; отсчёт высот
−0,015	чистый пол пом. 3, 4, ниже на 15 мм
−0,064*	верх плиты — расчёт, не замер (задание на обмер)
сущ. пол	снимается до плиты; не замерен (задание на обмер)

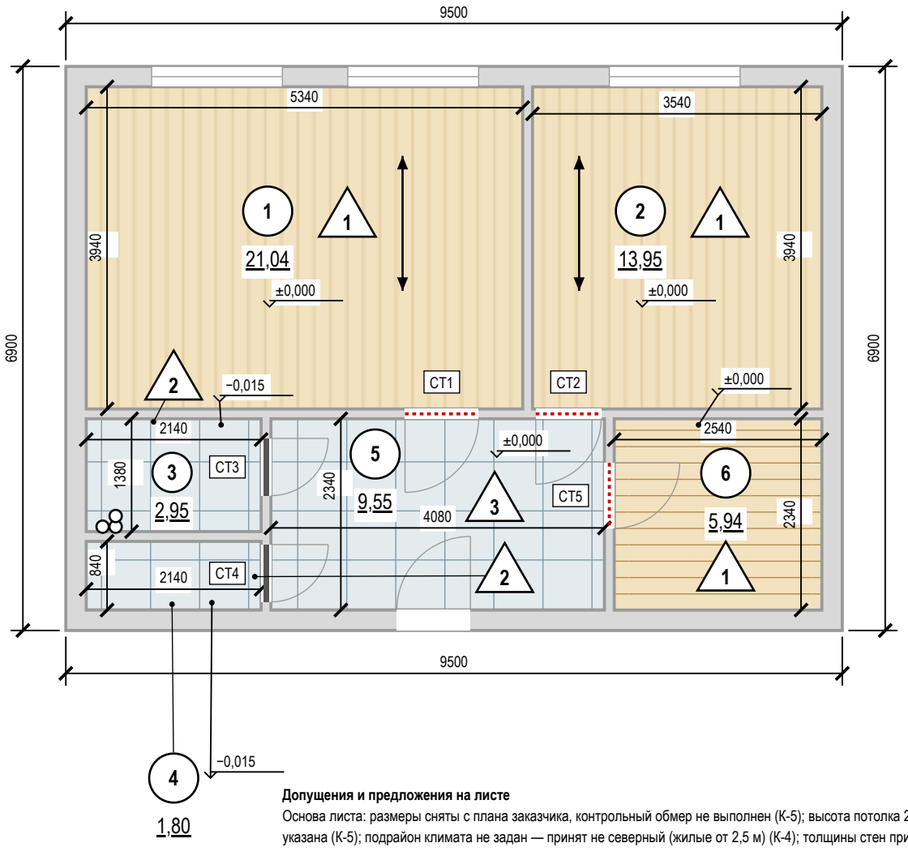




Допущения и предложения на листе

Основа листа: размеры сняты с плана заказчика, контрольный обмер не выполнен (К-5); высота потолка 2700 мм принята: на плане заказчика не указана (К-5); подрайон климата не задан — принят не северный (жилые от 2,5 м) (К-4); толщины стен приняты: наружные 250 мм, перегородки 120 мм — не обмерены (К-5); разрешённая мощность 15 кВт принята по типовой квартире, технических условий нет (К-6).

Знак «**» — предложение проектировщика, заказчиком не утверждено (согласовать с заказчиком): пол пом. 1, 2, 6 — артикул изделия не выбран: позиция описана характеристиками («аналог по характеристикам»), артикул выбирается при закупке.

См. лист открытых вопросов (лист 6, записи К-4–К-6).

Экспликация полов

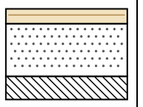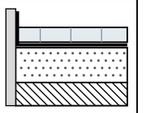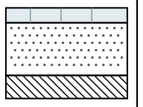Номер помещения	Тип пола	Схема пола	Данные элементов пола (наименование, толщина, основание), мм	Площадь, м²
1, 2, 6	1		Инженерная доска на клею — 14 Стяжка ЦПС М200 — 50 Плита перекрытия Всего 64 мм; ЧП ±0,000, верх плиты −0,064	40,93
3, 4	2		Керамогранит на клею С2 TE S1 — 14 Гидроизоляция обмазочная, 2 слоя, с заведением на стены 200 мм — 2 Стяжка ЦПС М200 — 33 Плита перекрытия Всего 49 мм; ЧП −0,015, верх плиты −0,064	4,75
5	3		Керамогранит на клею С2 TE S1 — 14 Стяжка ЦПС М200 — 50 Плита перекрытия Всего 64 мм; ЧП ±0,000, верх плиты −0,064	9,55
			Итого	**55,23**

Раскладка покрытий

Пом.	Укладка	Старт (оси от чистовых стен), мм	Отступ 1-го ряда / крайние плитки, мм
1	вдоль стен Б/Г, прямая	от стены Г, 1-й ряд вдоль неё	зазор от стены не задан
2	вдоль стен Б/Г, прямая	от стены Г, 1-й ряд вдоль неё	зазор от стены не задан
3	плитка	раскладка плиточника не задана	
4	плитка	раскладка плиточника не задана	
5	плитка	раскладка плиточника не задана	
6	вдоль стен А/В, прямая	от стены А, 1-й ряд вдоль неё	зазор от стены не задан

Стыки покрытий в проёмах

Марка	Проём	Типы пола	Отметки ЧП	Решение
СТ1	5–1 (Д-2)	3 / 1	±0,000 / ±0,000	не задано
СТ2	5–2 (Д-3)	3 / 1	±0,000 / ±0,000	не задано
СТ3	5–3 (Д-4)	3 / 2	±0,000 / −0,015	порог h=15 мм
СТ4	5–4 (Д-4)	3 / 2	±0,000 / −0,015	порог h=15 мм
СТ5	6–5 (Д-3)	1 / 3	±0,000 / ±0,000	не задано

Примечания

1. За отметку ±0,000 принят чистый пол, не существующий (блок отметок). Площади — по чистым размерам помещений, м²; размеры — в мм.
2. Стык разнотипных покрытий — по оси дверного полотна (под полотном в закрытом положении); решение стыка — по ведомости стыков.
3. Пол санузлов ниже смежных помещений на 15 мм за счёт меньшей толщины стяжки (верх плиты общий — по экспликации полов); гидроизоляция по стяжке с заведением на стены не менее 200 мм (СП 29.13330.2011, п. 7.2), до облицовки — тест проливом и акт скрытых работ.
4. Трубопроводы в конструкции пола не прокладываются: пирог пола 49–64 мм не вмещает выпуски канализации с уклоном — выпуски К1 ведутся по стенам над чистым полом в коробах (лист 39).
5. Звукоизоляционный слой под стяжкой проектом не предусмотрен (стяжка по плите): приведённый уровень ударного шума перекрытия с полом Lnw не более 60 дБ (СП 51.13330.2011, табл. 2) подтвердить по данным дома; при превышении — плавающая стяжка по звукоизоляции с демпферной лентой по контуру и у стояков, пирог пересчитать.
6. Штучные покрытия (инженерная доска): направление — по стрелке; влажность основания по СМ не более 2,0 % (по ТУ изготовителя).
7. Ровность основания — просвет под 2-метровой рейкой не более 2 мм: пом. 1, 2, 6 (инженерная доска), пом. 3, 4, 5 (керамогранит); проверить до укладки покрытия (СП 71.13330.2017, табл. 8.5).
8. Сетка на плитке — условная, в размер формата; точка старта и раскладка — по листу раскладки плитки.
9. Узор покрытия (заливка-код типа пола) прерывается под надписями — площадями помещений и отметками чистого пола.
10. Пироги полов — по экспликации полов: слои сверху вниз, толщины в мм; гидроизоляция мокрых зон — в пироге и в ведомости отделки; схема пола — без масштаба.

1000 мм · печать 1:1

Изм.	Кол.уч	Лист	№ док.	Подп.	Дата
Разраб.		Кырлан А.С.			14.11.26
Пров.					
ГИП					
Н. контр.					
Утв.					

ГД-2026-006-АИ

Квартира 58 м²

Общая площадь 55,23* м² · * размеры приняты, не замерены (реестр — л. 6, 7, К-5)

Дизайн-проект интерьера

Стадия	Лист	Листов
РП	55	108

План полов

М 1:75

Кырлан Александр Сергеевич

выпуск 14.11.2026 № bcee049e32 · стр. 62 из 128

Ведомость отделки помещений

Потолки, стены, низ стен, полы · площади в м², длины в м · отметки в м

Ведомость отделки помещений (форма 1 прил. А ГОСТ 21.501-2018)

№	Наименование помещения	Потолок			Стены и перегородки			Низ стен (плинтус)			Пол		Примечание
		Вид отделки	Код цвета	S, м²	Вид отделки	Код цвета	S, м²	Вид отделки	Код цвета	L, м	Вид отделки	S, м²	
1	Кухня-гостиная 21,04 м²	ГКЛ по каркасу П113, отм. +2,600; +2,550; окраска, Tikkurila, глубокоматовая	NCS S 0300-N	21,04	Окраска, Tikkurila, полуматовая, подготовка Q3	NCS S 1002-Y50R	41,25	Плинтус МДФ h=110 мм, SX184	NCS S 0300-N	17,7	Аналог: инженерная доска, дуб натуральный, масло, 1-полосная, 14/4 мм, на клею; тип 1, отм. ЧП ±0,000	21,04	Н стен 2600 (до потолка)
2	Спальня 13,95 м²	ГКЛ по каркасу П113, отм. +2,600; +2,550; окраска, Tikkurila, глубокоматовая	NCS S 0300-N	13,95	Окраска, Tikkurila, глубокоматовая, подготовка Q3	NCS S 1502-Y50R	33,91	Плинтус МДФ h=110 мм, SX184	NCS S 0300-N	14,2	Аналог: инженерная доска, дуб натуральный, масло, 1-полосная, 14/4 мм, на клею; тип 1, отм. ЧП ±0,000	13,95	Н стен 2550 (до потолка)
3	Ванная 2,95 м²	ГКЛВ по каркасу П113, отм. +2,600; окраска, Tikkurila, глубокоматовая	NCS S 0300-N	2,95	Облицовка плиткой, 610015000370, 600×1200 мм, клей С2	Italon 610015000370	16,94	нет (облицовка от пола)			Керамогранит, SG651622R, 600×600 мм; тип 2, отм. ЧП −0,015	2,95	Н стен 2615 (до потолка); тёплый пол; гидроизоляция обмазочная, 2 слоя, с заведением на стены 200 мм; над ванной — до 2000 и 300 мм за борт (по пирогу пола); тест проливом и акт скрытых работ
4	Санузел 1,80 м²	ГКЛВ по каркасу П113, отм. +2,600; окраска, Tikkurila, глубокоматовая	NCS S 0300-N	1,80	Облицовка плиткой, 610015000370, 600×1200 мм, клей С2	Italon 610015000370	14,12	нет (облицовка от пола)			Керамогранит, SG651622R, 600×600 мм; тип 2, отм. ЧП −0,015	1,80	Н стен 2615 (до потолка); гидроизоляция обмазочная, 2 слоя, с заведением на стены 200 мм (по пирогу пола); тест проливом и акт скрытых работ
5	Прихожая 9,55 м²	ГКЛ по каркасу П113, отм. +2,550; +2,600; окраска, Tikkurila, глубокоматовая	NCS S 0300-N	9,55	Окраска, Tikkurila, полуматовая, подготовка Q3	NCS S 1502-Y50R	22,66	Плинтус МДФ h=110 мм, SX184	NCS S 0300-N	8,0	Керамогранит, SG651622R, 600×600 мм; тип 3, отм. ЧП ±0,000	9,55	Н стен 2550 (до потолка)
6	Гардеробная 5,94 м²	Существующий потолок, отм. +2,700; окраска, Tikkurila Anti-Reflex 2, глубокоматовая, 2 слоя, подготовка Q3	Tikkurila V503	5,94	Окраска, Tikkurila Harmony, матовая, 2 слоя, подготовка Q3	Tikkurila V503	24,67	Плинтус МДФ h=110 мм, SX184	Tikkurila V503	9,0	Аналог: инженерная доска, дуб натуральный, масло, 1-полосная, 14/4 мм, на клею; тип 1, отм. ЧП ±0,000	5,94	Н стен 2700 (до потолка); плинтус в цвет: стены
	Итого			**55,23**			**153,54**			**48,8**		**55,23**	

Сводка площадей по материалам отделки

Поверхность	Материал / код цвета	Серия	Площадь, м²
Потолок	NCS S 0300-N		49,29
Потолок	Tikkurila V503	Anti-Reflex 2	5,94
Стены	NCS S 1002-Y50R		41,25
Стены	NCS S 1502-Y50R		56,57
Стены	облицовка плиткой 600×1200 мм, Italon 610015000370	610015000370	31,05
Стены	Tikkurila V503	Harmony	24,67

Допущения и предложения на листе

Основа листа: размеры сняты с плана заказчика, контрольный обмер не выполнен (К-5); высота потолка 2700 мм принята: на плане заказчика не указана (К-5); подрайон климата не задан — принят не северный (жилые от 2,5 м) (К-4); толщины стен приняты: наружные 250 мм, перегородки 120 мм — не обмерены (К-5); разрешённая мощность 15 кВт принята по типовой квартире, технических условий нет (К-6).

Знак «**» — предложение проектировщика, заказчиком не утверждено (согласовать с заказчиком): пол пом. 1, 2, 6 — артикул изделия не выбран: позиция описана характеристиками («аналог по характеристикам»), артикул выбирается при закупке.

См. лист открытых вопросов (лист 6, записи К-4–К-6).

Примечания

1. Площади поверхностей — по чистым граням стен до отделки: стены = периметр × высоту от чистого пола помещения до низа потолка минус проёмы (облицовка плиткой — до верха облицовки); плинтус = периметр минус дверные проёмы; пол и потолок — по площади помещения. Количество плиток по раскладке. Площади помещений — с учётом всех частей помещения; откосы в площадь стен не входят.
2. Акцентные стены — отдельными строками, их площадь вычтена из основной отделки стен помещения.
3. Плинтус — длина по периметру за вычетом дверных проёмов; примыкания к наличникам и встроенной мебели — по развёрткам.
4. Формат плитки — Ш×В×Т (ширина × высота в положении укладки × толщина), мм; на полу — вдоль стен А/В × вдоль стен Б/Г.
5. Коды цвета — по веерам производителей; колеровка каждой краски одной партией, проверка выкраса при свете D65 и при лампах проекта.
6. Уровни подготовки Q1–Q4 — система Knauf, не норма ГОСТ/СП; допуски поверхностей — по СП 71.13330.2017 (действующая редакция).
7. «аналог:» — изделие задано характеристиками, марку и артикул согласовать с заказчиком до закупки.

Изм.	Кол.уч	Лист	№ док.	Подп.	Дата
Разраб.		Кырлан А.С.			14.11.26
Пров.					
ГИП					
Н. контр.					
Утв.					

ГД-2026-006-АИ

Квартира 58 м²

Общая площадь 55,23* м² · * размеры приняты, не замерены (реестр — л. 6, 7, К-5)

Дизайн-проект интерьера

Стадия	Лист	Листов
РП	56	108

Ведомость отделки помещений

М б/м

Кырлан Александр Сергеевич

Колерная карта

Цвета и материалы по помещениям · палитра проекта · выкрасы на согласование

Колерная карта по помещениям

Помещение	Поверхность	Образец	Поз.	Система и код цвета	Производитель, линейка / материал, артикул	Блеск	Класс истирания	LRV	Площадь
1. Кухня-гостиная 21,04 м²	стены		**К1**	NCS S 1002-Y50R	Tikkurila	полуматов.	1	82	41,2 м²
	потолок		**К2**	NCS S 0300-N	Tikkurila	глубокомат.	1	92	21,0 м²
	пол		**КМ1**	по образцу	инженерная доска · аналог по хар.				21,0 м²
	плинтус		**К3**	NCS S 0300-N	Orac Decor · Luxxus	полуматов.		92	17,7 м
2. Спальня 13,95 м²	стены		**К4**	NCS S 1502-Y50R	Tikkurila	глубокомат.	2	72	33,9 м²
	потолок		**К5**	NCS S 0300-N	Tikkurila	глубокомат.	2	92	13,9 м²
	пол		**КМ1**	по образцу	инженерная доска · аналог по хар.				13,9 м²
	плинтус		**К3**	NCS S 0300-N	Orac Decor · Luxxus	полуматов.		92	14,2 м
3. Ванная 2,95 м²	стены		**КМ2**	Charme Extra	Italon · арт. 610015000370				16,9 м²
	потолок		**К2**	NCS S 0300-N	Tikkurila	глубокомат.	1	92	3,0 м²
	пол		**КМ3**	Две Венеции / Риальто	Kerama Marazzi · арт. SG651622R				3,0 м²
4. Санузел 1,8 м²	стены		**КМ2**	Charme Extra	Italon · арт. 610015000370				14,1 м²
	потолок		**К2**	NCS S 0300-N	Tikkurila	глубокомат.	1	92	1,8 м²
	пол		**КМ3**	Две Венеции / Риальто	Kerama Marazzi · арт. SG651622R				1,8 м²
5. Прихожая 9,55 м²	стены		**К6**	NCS S 1502-Y50R	Tikkurila	полуматов.	1	72	22,7 м²
	потолок		**К2**	NCS S 0300-N	Tikkurila	глубокомат.	1	92	9,6 м²
	пол		**КМ3**	Две Венеции / Риальто	Kerama Marazzi · арт. SG651622R				9,6 м²
	плинтус		**К3**	NCS S 0300-N	Orac Decor · Luxxus	полуматов.		92	8,0 м
6. Гардеробная 5,94 м²	стены		**К7**	Tikkurila V503	Tikkurila · Harmony	матовая	1	86	24,7 м²
	потолок		**К8**	Tikkurila V503	Tikkurila · Anti-Reflex 2	глубокомат.	2	86	5,9 м²
	пол		**КМ1**	по образцу	инженерная доска · аналог по хар.				5,9 м²
	плинтус		**К9**	Tikkurila V503	Orac Decor · Luxxus			86	9,0 м

Перечень выкрасов на согласование

№	Код	Бренд / веер	Пом. / стена	Подложка	Формат	Статус
1	S 1002-Y50R	NCS Tikkurila	1	ГКЛ с грунтом	600×1000	к выполнению
2	S 0300-N	NCS Tikkurila	1, 2, 3, 4, 5	ГКЛ с грунтом; МДФ под эмаль	600×1000; 300×600	к выполнению
3	S 1502-Y50R	NCS Tikkurila	2, 5	ГКЛ с грунтом	600×1000	к выполнению
4	V503	Tikkurila	6	ГКЛ с грунтом; МДФ под эмаль	600×1000; 300×600	к выполнению

Схема квартиры: цвет стен и акценты (б/м)

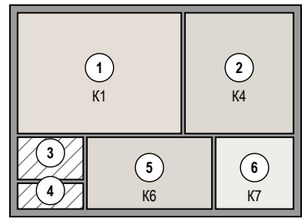


Схема палитры проекта


Стиль: Скандинавский · схема: нейтральная

основной	основной	основной	второстепенный	акцентный
NCS S 1502-Y50R	**NCS S 1002-Y50R**	**NCS S 0300-N**	**Tikkurila V503**	**NCS S 4010-R90B**
тёплый светло-серый LRV 72 стены 2,5	тёплый светлый грейж LRV 82 стены 1	белый LRV 92 потолок 1,2,3,4,5; плинтус 1,2,5	Winter LRV 86 стены 6; потолок 6; плинтус 6	пыльный синий LRV 27 текстиль/декор 1,2,3

План 60/30/10



Окраска, факт — по площади стен, акцентов, потолков

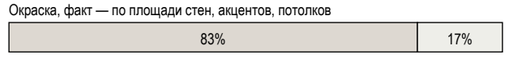

окрашено всего 177,7 м²; второстепенный тон несут мебель и текстиль

Текстиль и декор в цветах вне палитры проекта

- Tikkurila G503 Calla — пом. 1 (Т1**, Т2**, Т4**), 2 (Т7**), 3 (Т13**)
- NCS S 2002-Y серый камень, тёплый — пом. 1 (Т3**)
- NCS S 3010-G10Y шалфей средний — пом. 1 (Т6**), 2 (Т9**), 4 (ДК12**)
- Farrow & Ball No. 241 Skimming Stone — пом. 2 (Т8**)

Условные обозначения

- **К1** NCS S 1002-Y50R · Tikkurila · полуматов. · кл. 1
- **К2** NCS S 0300-N · Tikkurila · глубокомат. · кл. 1
- **К3** NCS S 0300-N · Orac Decor Luxxus · полуматов.
- **К4** NCS S 1502-Y50R · Tikkurila · глубокомат. · кл. 2
- **К5** NCS S 0300-N · Tikkurila · глубокомат. · кл. 2
- **К6** NCS S 1502-Y50R · Tikkurila · полуматов. · кл. 1
- **К7** Tikkurila V503 · Winter · Harmony · матовая · кл. 1
- **К8** Tikkurila V503 · Winter · Anti-Reflex 2 · глубокомат. · кл. 2
- **К9** Tikkurila V503 · Winter · Luxxus
- **КМ1** аналог: инженерная доска, дуб натуральный, масло, 1-полосная, 14/4 мм
- **КМ2** плитка · 610015000370
- **КМ3** керамогранит · SG651622R

дерево (доска, паркет, ламинат) — рисунок досок

керамогранит, плитка, камень — сетка швов по формату

плашка не залита — цвет только по коду и вееру бренда

К — краска, КМ — отделочный материал (тон КМ — по описанию, эталон — образец материала); кл. — класс истирания (1 — самый стойкий к мытью); LRV — светлота цвета: 0 — чёрный, 100 — белый

Примечания

1. Цвет на листе и на экране — ориентир. До покраски — выкрас на объекте: не меньше А3 (или лист ГКЛ), на грунте под эту краску, не на белой шпаклёвке, в 2 слоя; на обороте — код, бренд, веер, дата. Смотреть днём и вечером, рядом с образцами пола и плитки; к основному цвету стен — ещё 2 соседних оттенка. Красить только в цвет утверждённого выкраса.
2. Краску заказывать по коду из графы «Система и код цвета» у бренда этого кода, не «аналогом» другого; весь объём одного кода — одной партией, колеруемую краску — за один проход машины.
3. Площади — те же, что в ведомости отделки (лист 56); сколько краски заказать — в спецификации отделочных материалов (лист 58).

Допущения и предложения на листе

Основа листа: размеры сняты с плана заказчика, контрольный обмер не выполнен (К-5); высота потолка 2700 мм принята: на плане заказчика не указана (К-5); подрайон климата не задан — принят не северный (жилые от 2,5 м) (К-4); толщины стен приняты: наружные 250 мм, перегородки 120 мм — не обмерены (К-5); разрешённая мощность 15 кВт принята по типовой квартире, технических условий нет (К-6).

Знак «**» — предложение проектировщика, заказчиком не утверждено (согласовать с заказчиком): пол пом. 1, 2, 6 — артикул изделия не выбран: позиция описана характеристиками («аналог по характеристикам»), артикул выбирается при закупке; ИЗ-4: Т1, Т2, Т3, Т4, Т6, Т7, Т8, Т9; ИЗ-5: Т13, ДК12.

См. лист открытых вопросов (лист 6, записи К-4–К-6; лист 7, записи ИЗ-4, ИЗ-5).

Изм.	Кол.уч	Лист	№ док.	Подп.	Дата
Разраб.		Кырлан А.С.			14.11.26
Пров.					
ГИП					
Н. контр.					
Утв.					

ГД-2026-006-АИ

Квартира 58 м²

Общая площадь 55,23* м² · * размеры приняты, не замерены (реестр — л. 6, 7, К-5)

Дизайн-проект интерьера

Стадия	Лист	Листов
РП	57	108

Колерная карта

М б/м

Кырлан Александр Сергеевич

Спецификация отделочных материалов

ПРЕДВАРИТЕЛЬНО · не для производства работ · открыто пунктов: 9 (реестр — л. 6, 7)

Форма 1 по ГОСТ 21.110-2013 · количества — из геометрии проекта, с запасом · часть 1 из 2

Поз.	Наименование и техническая характеристика	Тип, марка, обозначение документа	Код продукции	Поставщик	Ед. изм.	Кол.	Масса 1 ед., кг	Примечание
	Лакокрасочные материалы							
1	Краска интерьерная водно-дисперсионная акриловая для стен, полуматовая, класс мокрого истирания 1 по EN 13300, база A; цвет NCS S 1002-Y50R, колеровка машинная	Tikkurila		Tikkurila	л	11,7		поз. К1 колерной карты; пом. 1; S = 41,2 м² × 2 сл. × 0,12 л/м² = 9,9 л, +10 % и 0,5 л на подкраску → ≥ 11,4 л; тара 1 × 9 л + 1 × 2,7 л
2	Краска интерьерная водно-дисперсионная для потолков, глубокоматовая, класс мокрого истирания 1 по EN 13300, база A; цвет NCS S 0300-N, колеровка машинная	Tikkurila		Tikkurila	л	9,9		поз. К2 колерной карты; пом. 1, 3, 4, 5; S = 35,3 м² × 2 сл. × 0,12 л/м² = 8,5 л, +10 % и 0,5 л на подкраску → ≥ 9,8 л; тара 1 × 9 л + 1 × 0,9 л
3	Краска интерьерная водно-дисперсионная акриловая для стен, глубокоматовая, класс мокрого истирания 2 по EN 13300, база A; цвет NCS S 1502-Y50R, колеровка машинная	Tikkurila		Tikkurila	л	9,9		поз. К4 колерной карты; пом. 2; S = 33,9 м² × 2 сл. × 0,12 л/м² = 8,1 л, +10 % и 0,5 л на подкраску → ≥ 9,5 л; тара 1 × 9 л + 1 × 0,9 л
4	Краска интерьерная водно-дисперсионная для потолков, глубокоматовая, класс мокрого истирания 2 по EN 13300, база A; цвет NCS S 0300-N, колеровка машинная	Tikkurila		Tikkurila	л	4,5		поз. К5 колерной карты; пом. 2; S = 13,9 м² × 2 сл. × 0,12 л/м² = 3,3 л, +10 % и 0,5 л на подкраску → ≥ 4,2 л; тара 1 × 2,7 л + 2 × 0,9 л
5	Краска интерьерная водно-дисперсионная акриловая для стен, полуматовая, класс мокрого истирания 1 по EN 13300, база A; цвет NCS S 1502-Y50R, колеровка машинная	Tikkurila		Tikkurila	л	7,2		поз. К6 колерной карты; пом. 5; S = 22,7 м² × 2 сл. × 0,12 л/м² = 5,4 л, +10 % и 0,5 л на подкраску → ≥ 6,5 л; тара 2 × 2,7 л + 2 × 0,9 л
6	Краска интерьерная водно-дисперсионная акриловая для стен, матовая, класс мокрого истирания 1 по EN 13300, база A; цвет по вееру Tikkurila V503 «Winter», колеровка машинная	Tikkurila Harmony		Tikkurila	л	7,2		поз. К7 колерной карты; пом. 6; S = 24,7 м² × 2 сл. × 0,12 л/м² = 5,9 л, +10 % и 0,5 л на подкраску → ≥ 7,0 л; тара 2 × 2,7 л + 2 × 0,9 л
7	Краска интерьерная водно-дисперсионная акриловая для потолков, глубокоматовая, класс мокрого истирания 2 по EN 13300, база A; цвет по вееру Tikkurila V503 «Winter», колеровка машинная	Tikkurila Anti-Reflex 2		Tikkurila	л	2,7		поз. К8 колерной карты; пом. 6; S = 5,9 м² × 2 сл. × 0,12 л/м² = 1,4 л, +10 % и 0,5 л на подкраску → ≥ 2,1 л; тара 1 × 2,7 л
8	Акрил, полуматовая в цвет NCS S 0300-N — окраска плинтуса	аналог по характеристикам			л	1,4		поз. К3; пом. 1, 2, 5; L = 39,9 м, S = 5,0 м² × 2 сл. × 0,12 л/м² + 10 %; продукт подобрать в веере NCS
9	Краска для МДФ и дерева в цвет Tikkurila V503 «Winter» — окраска плинтуса; блеск не ниже блеска стен	марка не задана			л	0,5		поз. К9; пом. 6; L = 9,0 м, S = 1,1 м² × 2 сл. × 0,12 л/м² + 10 %; продукт подобрать в веере Tikkurila
10	Грунтовка акриловая под окраску стен и потолков — из системы производителя краски	по системе краски			м²	178		площадь окраски стен, акцентов и потолков; 1 слой перед окраской; расход — по ТУ грунтовки

Допущения и предложения на листе

Основа листа: размеры сняты с плана заказчика, контрольный обмер не выполнен (К-5); высота потолка 2700 мм принята: на плане заказчика не указана (К-5); подрайон климата не задан — принят не северный (жилые от 2,5 м) (К-4); толщины стен приняты: наружные 250 мм, перегородки 120 мм — не обмерены (К-5); разрешённая мощность 15 кВт принята по типовой квартире, технических условий нет (К-6).

Знак «**» — предложение проектировщика, заказчиком не утверждено (согласовать с заказчиком): пол пом. 1, 2, 6 — артикул изделия не выбран: позиция описана характеристиками («аналог по характеристикам»), артикул выбирается при закупке.

См. лист открытых вопросов (лист 6, записи К-4–К-6).

Изм.	Кол.уч	Лист	№ док.	Подп.	Дата
Разраб.		Кырлан А.С.			14.11.26
Пров.					
ГИП					
Н. контр.					
Утв.					

ГД-2026-006-АИ

Квартира 58 м²

Общая площадь 55,23* м² · * размеры приняты, не замерены (реестр — л. 6, 7, К-5)

Дизайн-проект интерьера

Стадия	Лист	Листов
РП	58	108

Спецификация отделочных материалов

М б/м

Кырлан Александр Сергеевич

Спецификация отделочных материалов

ПРЕДВАРИТЕЛЬНО · не для производства работ · открыто пунктов: 9 (реестр — л. 6, 7)

Форма 1 по ГОСТ 21.110-2013 · количества — из геометрии проекта, с запасом · часть 2 из 2

Поз.	Наименование и техническая характеристика	Тип, марка, обозначение документа	Код продукции	Поставщик	Ед. изм.	Кол.	Масса 1 ед., кг	Примечание
	Плитка и керамогранит							
11	SG651622R, 600×600 мм, противоскольжение R10	SG651622R		Kerama Marazzi	м²	19,44		шов 2 мм; Ванная, пол; Санузел, пол; Прихожая, пол; по раскладке 48 шт (S = 14,30 м²), с запасом 54 шт
12	610015000370, 1200×600 мм	610015000370		Italon	м²	70,56		шов 2 мм; Ванная, стены А–Г; Ванная, короб стояков Ш1 489×319; Санузел, стены А–Г; Санузел, короб инсталляции; по раскладке 87 шт (S = 31,81 м²), с запасом 98 шт
	Напольные покрытия							
13	Инженерная доска, дуб натуральный, масло, 1-полосная, 14/4 мм, класс 33, эмиссия E1, укладка на клей	аналог по характеристикам			м²	37,6		пом. 1, 2; S = 35,12 м² (пол + половина стены в дверных проёмах, как в смете) + 7 %; к заказу — кратно упаковке
14	Инженерная доска, дуб натуральный, масло, 1-полосная, 14/4 мм, эмиссия E1, укладка на клей	аналог по характеристикам			м²	6,4		пом. 6; S = 5,96 м² (пол + половина стены в дверных проёмах, как в смете) + 7 %; к заказу — кратно упаковке
15	Клей для паркета и инженерной доски, эластичный (СМП / полиуретановый)	по рекомендации производителя доски			м²	42		площадь приклейки; расход и шпатель — по ТУ клея
	Погонажные изделия							
16	SX184, h = 110 мм, крепление к стене, окраска в цвет NCS S 0300-N	SX184		Orac Decor	м	44		пом. 1, 2, 5; L = 39,9 м (периметр без дверных проёмов) + 10 % на подрезку; в штуках — по длине планки
17	SX184, h = 110 мм, крепление к стене, окраска в цвет Tikkurila V503	SX184		Orac Decor	м	10		пом. 6; L = 9,0 м (периметр без дверных проёмов) + 10 % на подрезку; в штуках — по длине планки
	Смеси и материалы для облицовки							
18	Затирка для швов плитки	аналог по характеристикам			кг	3,9		по раскладке (a+b)/(a·b) × шов × t × 1,6 + 10 %
19	Клей плиточный C2 S1 по EN 12004, слой 5 мм	аналог по характеристикам			кг	28		2 меш. по 25 кг; 1,5 кг/м² на 1 мм слоя + 10 %
20	Клей плиточный C2 по EN 12004, слой 5 мм	аналог по характеристикам			кг	266		11 меш. по 25 кг; 1,5 кг/м² на 1 мм слоя + 10 %
21	Гидроизоляция обмазочная мокрых зон: пол, стены по периметру, зоны замачивания; 2 слоя с армирующей лентой в углах	аналог по характеристикам			м²	7,8		площадь по листу раскладки плитки + 10 %; расход смеси — по ТУ
22	Лента демпферная по периметру пола из плитки	аналог по характеристикам			м	21		периметр без дверных проёмов + 10 %

Примечания

1. Количества — из геометрии проекта: площади поверхностей по чистым граням стен до отделки (те же, что в ведомости отделки и колерной карте), плитка, клей и затирка — по раскладке плиточника; в графе «Кол.» — к заказу, с запасом.
2. Краска: расход 0,12 л/м² на слой в 2 слоя, если по ТУ не задан иной; запас 10 % и 0,5 л на подкраску каждого кода. Один код — одна партия, колеровка машинная в колеровочном центре бренда; в заказ — только после утверждения выкраса (колерная карта). Фасовка — по каталогу бренда на дату выпуска; к заказу — не меньше расчётного объёма.
3. «Аналог по характеристикам» — допускается изделие другого производителя с характеристиками не ниже указанных, по согласованию с автором проекта.
4. Графы «Код продукции» и «Масса 1 ед.» не заполнены: коды по классификатору продукции не присвоены, масса единицы до 25 кг (ГОСТ 21.110-2013).
5. Грунтовка и клей для доски указаны площадью обработки; объём — по ТУ выбранного продукта.

Допущения и предложения на листе

Основа листа: размеры сняты с плана заказчика, контрольный обмер не выполнен (К-5); высота потолка 2700 мм принята: на плане заказчика не указана (К-5); подрайон климата не задан — принят не северный (жилые от 2,5 м) (К-4); толщины стен приняты: наружные 250 мм, перегородки 120 мм — не обмерены (К-5); разрешённая мощность 15 кВт принята по типовой квартире, технических условий нет (К-6).

Знак «**» — предложение проектировщика, заказчиком не утверждено (согласовать с заказчиком): пол пом. 1, 2, 6 — артикул изделия не выбран: позиция описана характеристиками («аналог по характеристикам»), артикул выбирается при закупке.

См. лист открытых вопросов (лист 6, записи К-4–К-6).

Изм.	Кол.уч	Лист	№ док.	Подп.	Дата
Разраб.		Кырлан А.С.			14.11.26
Пров.					
ГИП					
Н. контр.					
Утв.					

ГД-2026-006-АИ

Квартира 58 м²

Общая площадь 55,23* м² · * размеры приняты, не замерены (реестр — л. 6, 7, К-5)

Дизайн-проект интерьера

Стадия	Лист	Листов
РП	59	108

Спецификация отделочных материалов

М б/м

Кырлан Александр Сергеевич


Концепция декора и визуализации

Скандинавский · кухня-гостиная и спальня · визуализации, палитра, материалы, ключевые предметы

место под визуализацию: вид сверху (3D) с мебелью, текстилем и декором


Вид сверху (3D) — визуализация в работе

Расстановка — по плану мебели (лист 24); шторы, ковры, картины и растения — по плану текстиля и декора (лист 61).

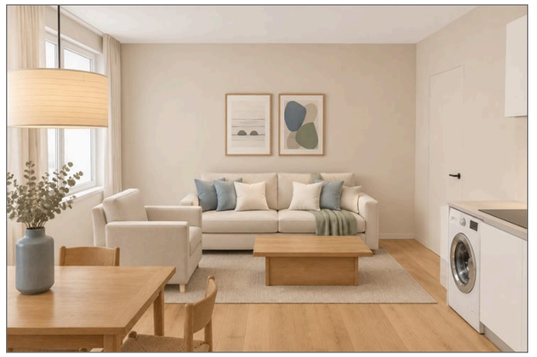

Визуализация 6. Кухня-гостиная (пом. 1)

шторы Т1**, Т2** · ковёр Т3** · картины ДК1**, ДК2** · растение ДК3** · подушки, пледы Т4**, Т5**, Т6**

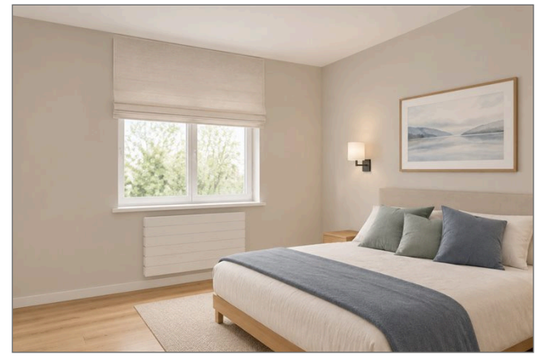

Визуализация 3. Спальня (пом. 2)

шторы Т7** · ковёр Т8** · картина ДК5** · зеркало ДК6** · растение ДК7** · подушки, пледы Т9**, Т10**, Т11**



Визуализация 1. Ванная (пом. 3)

ковёр Т14** · зеркало ДК8** · подушки, пледы Т12**, Т13**



Визуализация 10. Санузел (пом. 4)

картина ДК9**

Материалы и фактуры



Дуб натуральный

пол: пом. 1, 2, 6; рамы ДК1**, ДК2**, ДК5**, ДК6**, ДК10**, ДК11**




Букле

подушки: Т4**, Т10**




Лён

портьеры, подушки, римская штора: Т1**, Т2**, Т5**, Т7**, Т9**, Т12**, Т13**

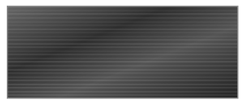

Чёрный матовый металл

рамы ДК9** — чёрный

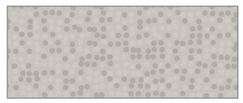

Шерсть

ковры, пледы: Т3**, Т6**, Т8**, Т11**, Т14**

Палитра 60/30/10 и цвета текстиля



- NCS S 1502-Y50R (тёплый светло-серый), LRV 72 — 60 % база
- Tikkurila V503 (Winter), LRV 86 — 30 % второй цвет
- Tikkurila G503 (Calla), LRV 89 — текстиль — Т1, Т2, Т4, Т7, Т13
- NCS S 3010-G10Y (шалфей средний), LRV 38 — текстиль — Т6, Т9
- NCS S 1002-Y50R (тёплый светлый грейж), LRV 82 — 60 % база
- NCS S 4010-R90B (пыльный синий), LRV 27 — 10 % акцент — Т5, Т10, Т11, Т12, Т14
- NCS S 2002-Y (серый камень, тёплый), LRV 55 — текстиль — Т3
- Farrow & Ball No. 241 (Skimming Stone), LRV 67 — текстиль — Т8

Ключевые предметы

— Диван М1** 2200×950 — кухня-гостиная; подушки и плед Т4**, Т5**, Т6**
— Кровати С1 — над изголовьем картины ДК5**; текстиль Т9**, Т10**, Т11**
— Ковры Т3**, Т8**, Т14** — шерсть, хлопок тафтинг, на противоскользящей подложке
— Картины ДК1**, ДК2**, ДК5**, ДК9**, ДК11** — центр на высоте 1450–1550 мм
— Зеркала в рост ДК6**, ДК10**; над умывальниками ДК8**
— Шторы-волна Т1**, Т2** (Tikkurila G503)
— Растение ДК3**, ваза ДК4**, растение ДК7**, ваза ДК12**

Допущения и предложения на листе. Основа листа: размеры сняты с плана заказчика, контрольный обмер не выполнен (К-5); высота потолка 2700 мм принята: на плане заказчика не указана (К-5); подрайон климата не задан — принят не северный (жилые от 2,5 м) (К-4); толщины стен приняты: наружные 250 мм, перегородки 120 мм — не обмерены (К-5); разрешённая мощность 15 кВт принята по типовой квартире, технических условий нет (К-6). Знак «**» — предложение проектировщика, заказчиком не утверждено (согласовать с заказчиком): ИЗ-2, ИЗ-4: М1 — Было offset 1300…3500: торец дивана в 500 мм от стены В, правые 350 мм проёма Д-2 (3900…4800) упирались в диван. См. лист открытых вопросов (лист 6, записи К-4–К-6; лист 7, записи ИЗ-2, ИЗ-4, ИЗ-5).

Настроение

Палитра выведена из выкрасов (колерная карта): база — тёплые нейтрали NCS S 1502-Y50R / S 1002-Y50R на стенах, NCS S 0300-N на потолках; второй цвет — Tikkurila V503 (гардеробная); акцент — пыльный синий NCS S 4010-R90B в текстиле по концепции стиля (ИЗ-4). Настроение стиля: светло, спокойно, уютно (hygge), естественно, функционально, в меру (lagom). Свет тёплый, 2700–3000 K.

Примечания

1. Визуализации — образ интерьера. Изделия, размеры, высоты подвеса и привязки — по чертежам (план текстиля и декора — лист 61; шторы и карнизы — лист 62; ведомость текстиля — лист 63; ведомость декора и развеска — лист 64); при расхождении действуют чертежи и ведомости.
2. Коды цвета — ориентир подбора по веерам производителей; ткань утверждается по образцу при дневном свете и при свете проекта 2700–3000 K.
3. Мелкий стайлинг на визуализациях (книги, посуда, свечи) в ведомости не входит и поставляется заказчиком по желанию.

Изм.	Кол.уч	Лист	№ док.	Подп.	Дата
Разраб.		Кырлан А.С.			14.11.26
Пров.					
ГИП					
Н. контр.					
Утв.					

ГД-2026-006-АИ

Квартира 58 м²

Общая площадь 55,23* м² · * размеры приняты, не замерены (реестр — л. 6, 7, К-5)

Дизайн-проект интерьера	Стадия	Лист	Листов
	РП	60	108

Концепция декора и визуализации

М б/м


Кырлан Александр Сергеевич

выпуск 14.11.2026 № bcee049e32 · стр. 67 из 128

План текстиля и декора

Шторы и карнизы, ковры, картины и зеркала, растения · размеры в мм от чистовых стен и чистого пола · марки — по ведомостям

ПРЕДВАРИТЕЛЬНО · не для производства работ · открыто пунктов: 9 (реестр — л. 6, 7)

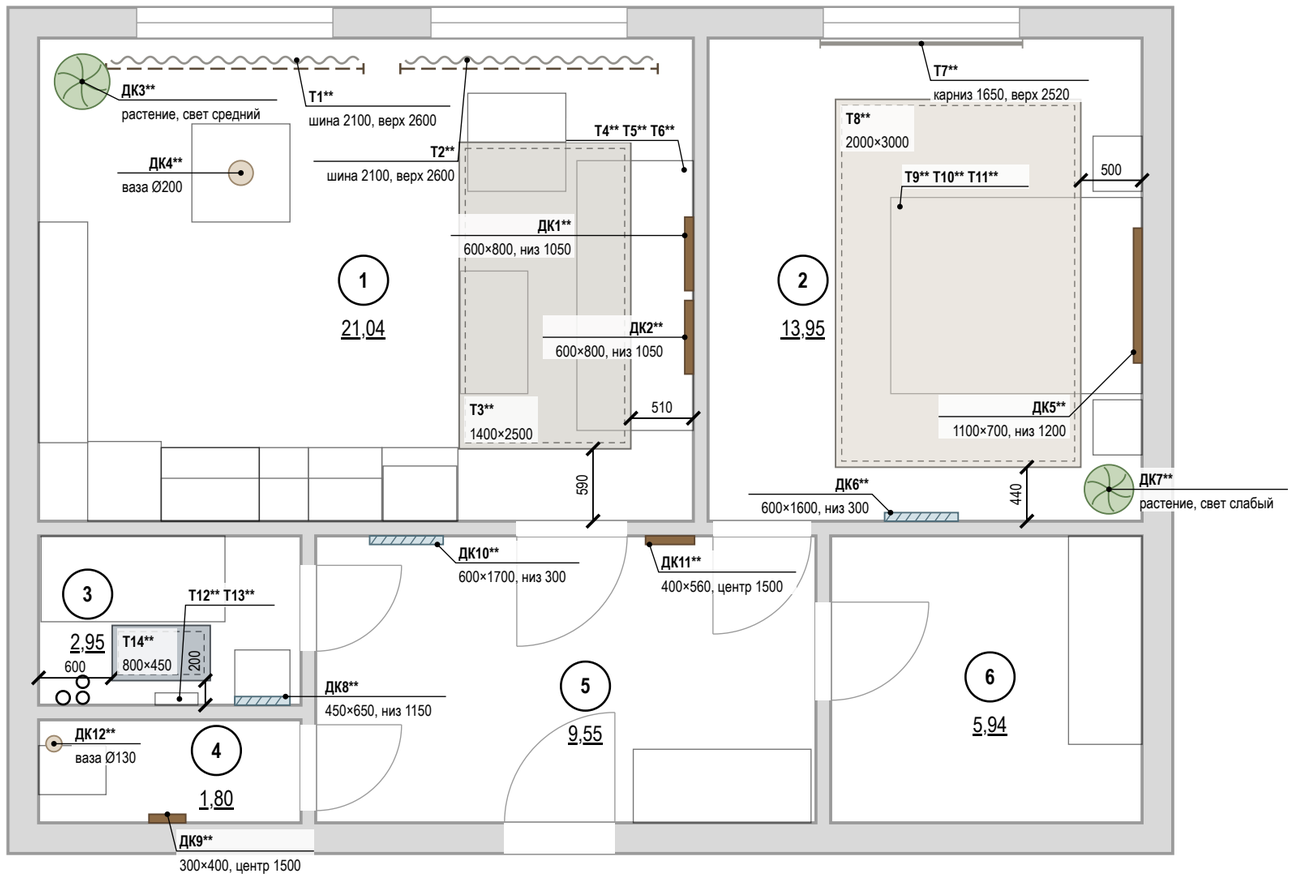

Условные обозначения

- ковёр — габарит в масштабе, цвет изделия
- шина или карниз штор (выше плоскости разреза)
- портьеры (штора-волна)
- тюль (на плане — волнистая линия)
- римская или рулонная штора в проёме
- картина на стене — ширина в масштабе
- зеркало на стене — ширина в масштабе
- растение в кашпо — диаметр в масштабе
- ваза, настольный декор
- подушки, пледы — марка на выноске к своей мебели
- привязка от чистовой стены, мм
- (1) номер помещения, площадь м²
- стены (подложка обмера)

Т1, ДК1 — марки по ведомостям текстиля и декора

Экспликация помещений

лист 20 · на плане — номера в марках

Окна: шина → полотно, мм

Поз.	Шина	Верх шины	Полотно, низ
Т1**	2100	2600	2590, низ 10
Т2**	2100	2600	2590, низ 10
Т7**	1650	2520	1750, низ 770

Развеска: высоты от пола, мм

Поз.	Пом.	Ш×В	Центр	Низ	Стена
ДК1**	1	600×800	1450	1050	Б
ДК2**	1	600×800	1450	1050	Б
ДК5**	2	1100×700	1550	1200	Б
ДК6**	2	600×1600	1100	300	В
ДК8**	3	450×650	1475	1150	В
ДК9**	4	300×400	1500	1300	В
ДК10**	5	600×1700	1150	300	А
ДК11**	5	400×560	1500	1220	А

Допущения и предложения на листе

Основа листа: размеры сняты с плана заказчика, контрольный обмер не выполнен (К-5); высота потолка 2700 мм принята: на плане заказчика не указана (К-5); подрайон климата не задан — принят не северный (жилые от 2,5 м) (К-4); толщины стен приняты: наружные 250 мм, перегородки 120 мм — не обмерены (К-5); разрешённая мощность 15 кВт принята по типовой квартире, технических условий нет (К-6).

Знак «**» — предложение проектировщика, заказчиком не утверждено (согласовать с заказчиком): ИЗ-4: Т1, Т2, Т3, Т4, Т5, Т6, ДК1, ДК2, ДК3, ДК4, Т7, Т8, Т9, Т10, Т11, ДК5, ДК6, ДК7, ДК8, ДК9, ДК10, ДК11; ИЗ-5: Т12, Т13, Т14, ДК12.

Изменения по листу без подписи: ИЗ-4, ИЗ-5.

См. лист открытых вопросов (лист 6, записи К-4–К-6; лист 7, записи ИЗ-4, ИЗ-5).

Примечания

1. Размеры — в мм. Отступы ковров — от чистовых стен; высоты картин и зеркал — от чистого пола до центра или низа рамы.
2. Шторы в пол — на шинах на потолке, без ниши; крепление к потолку — в перекрытие, при подшивном или натяжном потолке — в закладную до его монтажа. Римские шторы — на карнизах на стене над проёмом. Схемы окон, длины полотен и сборка — лист 62.
3. Картины и зеркала массой более 5 кг — на анкеры по основанию, нагрузка крепежа не меньше двойной массы изделия; на ГКЛ — только по закладной. Декор не перекрывает розетки и выключатели.
4. Ковры на гладком полу — на противоскользящей подложке.
5. Мебель — по плану расстановки мебели (лист 24); ведомость текстиля — лист 63, ведомость декора и схемы развески — лист 64.
6. Номера помещений — по экспликации (лист 20); наименования и площади на этом листе не дублируются.
7. Марки текстиля «Т» и декора «Д» относятся только к листам текстиля и декора; индексы трубопроводов Т1–Т4 — на листах ВК и ОВ.

1000 мм · печать 1:1

Изм.	Кол.уч	Лист	№ док.	Подп.	Дата
Разраб.		Кырлан А.С.			14.11.26
Пров.					
ГИП					
Н. контр.					
Утв.					

ГД-2026-006-АИ

Квартира 58 м²

Общая площадь 55,23* м² · * размеры приняты, не замерены (реестр — л. 6, 7, К-5)

Дизайн-проект интерьера

Стадия	Лист	Листов
РП	61	108

План текстиля и декора

М 1:50

Кырлан Александр Сергеевич

выпуск 14.11.2026 № bcee049e32 · стр. 68 из 128

08

Декор и текстиль


Кырлан Александр Сергеевич

выпуск 14.11.2026 № bcee049e32 · стр. 69 из 128


Шторы и карнизы

Схемы окон «шина → полотно» (М 1:50) · отметки от чистого пола помещения · размеры в мм


Окно 1 — Кухня-гостиная (пом. 1): Т1 (М 1:50)**

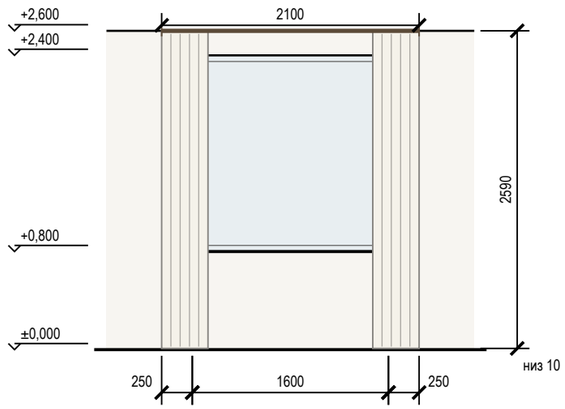

Окно 2 — Кухня-гостиная (пом. 1): Т2 (М 1:50)**

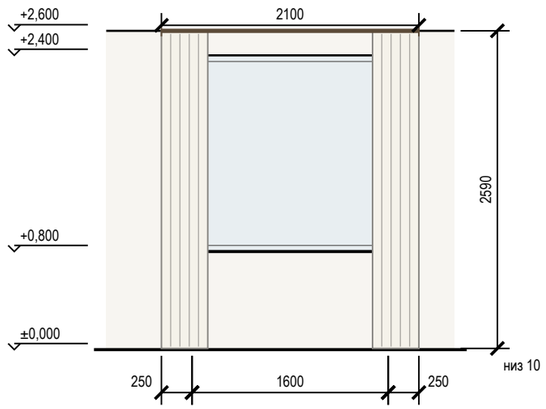

Окно 1 — Спальня (пом. 2): Т7 (М 1:50)**

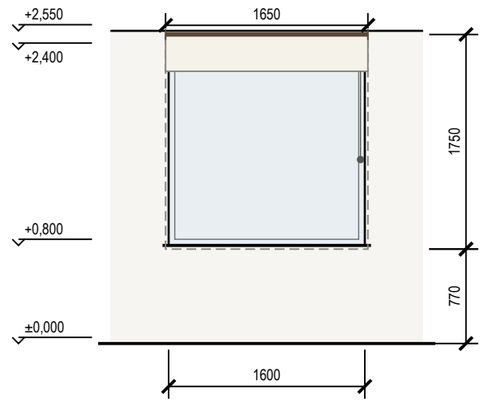

Карта окон: окно → шина → полотно

Поз.	Окно, пом.	Проём Ш×В, подоконник	Верх ниши	Изделие	Шина / карниз: длина, крепление	Верх шины	Полотно: длина, низ	Управление
Т1**	1, пом. 1	1600×1600, подок. 800		портьеры	шина, 2100, на потолок, вынос 250	+2,600	2590, низ 10 (парит)	вручную
Т2**	2, пом. 1	1600×1600, подок. 800		портьеры	шина, 2100, на потолок, вынос 250	+2,600	2590, низ 10 (парит)	вручную
Т7**	1, пом. 2	1600×1600, подок. 800		римская штора	карниз, 1650, на стену, вынос 60	+2,520	1750, низ 770	шнур, петля низом 1500, натяжитель

Задания смежникам

Кому	Задание	Пом.
Электрик	выводы под электрокарнизы не требуются (управление вручную)	

Условные обозначения

- портьеры в открытом положении
- римская штора: сложена / опущена
- верх ниши под шторы в потолке
- тюль (на виде окна — прозрачная плашка)
- шина или карниз на отметке верха
- оконный проём

Допущения и предложения на листе

Основа листа: размеры сняты с плана заказчика, контрольный обмер не выполнен (К-5); высота потолка 2700 мм принята: на плане заказчика не указана (К-5); подрайон климата не задан — принят не северный (жилые от 2,5 м) (К-4); толщины стен приняты: наружные 250 мм, перегородки 120 мм — не обмерены (К-5); разрешённая мощность 15 кВт принята по типовой квартире, технических условий нет (К-6).

Знак «**» — предложение проектировщика, заказчиком не утверждено (согласовать с заказчиком): ИЗ-4: Т1, Т2, Т7.

Изменения по листу без подписи: ИЗ-4.

См. лист открытых вопросов (лист 6, записи К-4–К-6; лист 7, запись ИЗ-4).

Примечания

1. Отметки — от чистого пола помещения; размеры — мм.
2. Шины и карнизы на потолке без ниши (Т1**, Т2**): крепление — в перекрытие; при подшивном или натяжном потолке — в закладную до его монтажа.
3. Карнизы на стене над проёмом (Т7**) — на анкеры по основанию; на ГКЛ — только по закладной.
4. Полотно портьер «парит» над полом на 10 мм; сборка портьер — 2,0, тюля — 2,5 (ширина полотна — в ведомости текстиля).
5. Шнур римской шторы — с натяжителем, петля низом не ниже 1500 мм от пола (защита детей; EN 13120 — рекомендация).
6. Электрокарнизы не предусмотрены; при замене на электропривод — вывод кабеля у края шины (задание электрику).
7. Марки изделий — по плану текстиля и декора (лист 61) и ведомости текстиля (лист 63).

Изм.	Кол.уч	Лист	№ док.	Подп.	Дата
Разраб.		Кырлан А.С.			14.11.26
Пров.					
ГИП					
Н. контр.					
Утв.					

ГД-2026-006-АИ

Квартира 58 м²

Общая площадь 55,23* м² · * размеры приняты, не замерены (реестр — л. 6, 7, К-5)

Дизайн-проект интерьера

Стадия	Лист	Листов
РП	62	108

Шторы и карнизы

М б/м

Кырлан Александр Сергеевич

Ведомость текстиля

Шторы, тюль, римские шторы, ковры, подушки и пледы · размеры в мм · марки — по плану текстиля и декора

Текстиль: шторы, ковры, подушки, пледы


Поз.	Пом.	Изделие	Размер, мм	Ткань, состав, плотность	Сборка, ширина полотна		Цвет (система, код)	Кол.	Примечание
T1**	1	Шторы льняные в пол, молочные (окно 1)	шина 2100 × полотно 2590	лён умягчённый, полупрозрачный; лён 100 %; 180 г/м²	× 2, ширина 4200		Tikkurila G503 (Calla)	2	низ 10 (парит); на потолок
T2**	1	Шторы льняные в пол, молочные (окно 2)	шина 2100 × полотно 2590	лён умягчённый, полупрозрачный; лён 100 %; 180 г/м²	× 2, ширина 4200		Tikkurila G503 (Calla)	2	низ 10 (парит); на потолок
T3**	1	Ковёр шерстяной плоского плетения 1400×2500, овсяный	1400×2500	шерсть, плоское плетение; шерсть 100 %			NCS S 2002-Y (серый камень, тёплый)	1	противоскользящая подложка; ворс 6 мм
T4**	1	Подушки на диван, букле молочное	500×500	букле (шерсть 60 %, полиэстер 40 %)			Tikkurila G503 (Calla)	3	на M1**
T5**	1	Подушки на диван, лён, пыльный синий	400×600	лён 100 %			NCS S 4010-R90B (пыльный синий)	2	на M1**
T6**	1	Плед шерстяной на диван, шалфей	1300×1700	шерсть мериноса 100 %			NCS S 3010-G10Y (шалфей средний)	1	на M1**
T7**	2	Римская штора льняная с блэкаут-подкладкой, молочная	карниз 1650 × полотно 1750	лён с блэкаут-подкладкой; лён 100 %			Tikkurila G503 (Calla)	1	низ 770; на стену; шнур: петля 1500, натяжитель
T8**	2	Ковёр шерстяной 2000×3000 под кроватью, светлый каменный	2000×3000	шерсть, плоское плетение; шерсть 100 %			Farrow & Ball No. 241 (Skimming Stone)	1	противоскользящая подложка; ворс 6 мм
T9**	2	Подушки декоративные на кровать, лён, шалфей	500×500	лён 100 %			NCS S 3010-G10Y (шалфей средний)	2	на C1
T10**	2	Подушка-валик на кровать, букле, пыльный синий	350×550	букле (шерсть 60 %, полиэстер 40 %)			NCS S 4010-R90B (пыльный синий)	1	на C1
T11**	2	Плед шерстяной крупной вязки в изножье кровати, пыльный синий	1300×1700	шерсть мериноса 100 %			NCS S 4010-R90B (пыльный синий)	1	на C1
T12**	3	Полотенца банные махровые, пыльный синий, сложены на полотенцесушителе	700×1400	махра; хлопок 100 %; 550 г/м²			NCS S 4010-R90B (пыльный синий)	2	на П5; уход: 40 °C, без кондиционера
T13**	3	Полотенца для рук вафельные, молочные, на нижних перекладинах сушителя	500×900	вафельное полотно; хлопок 100 %; 280 г/м²			Tikkurila G503 (Calla)	2	на П5; уход: 60 °C
T14**	3	Коврик для ванной у бортика ванны, хлопок тафтинг, пыльный синий	800×450	хлопок 100 %, латексная противоскользящая основа			NCS S 4010-R90B (пыльный синий)	1	противоскользящая подложка; ворс 12 мм; уход: 40 °C

образец цвета — по HEX производителя краски, справочно

Итого: шторы и тюль — 5 шт.; ковры и дорожки — 3 шт.; подушки, пледы, покрывала — 14 шт.


Образцы по помещениям

1. Кухня-гостиная

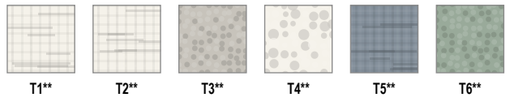

T1** T2** T3** T4** T5** T6**

2. Спальня

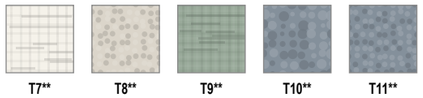

T7** T8** T9** T10** T11**

3. Ванная



T12** T13** T14**

Допущения и предложения на листе

Основа листа: размеры сняты с плана заказчика, контрольный обмер не выполнен (К-5); высота потолка 2700 мм принята: на плане заказчика не указана (К-5); подрайон климата не задан — принят не северный (жилые от 2,5 м) (К-4); толщины стен приняты: наружные 250 мм, перегородки 120 мм — не обмерены (К-5); разрешённая мощность 15 кВт принята по типовой квартире, технических условий нет (К-6).

Знак «**» — предложение проектировщика, заказчиком не утверждено (согласовать с заказчиком): ИЗ-2, ИЗ-4: M1 — Было offset 1300…3500: торец дивана в 500 мм от стены В, правые 350 мм проёма Д-2 (3900…4800) упирались в диван; ИЗ-4: T1, T2, T3, T4, T5, T6, T7, T8, T9, T10, T11; ИЗ-5: T12, T13, T14.

Изменения по листу без подписи: ИЗ-4, ИЗ-5.

См. лист открытых вопросов (лист 6, записи К-4–К-6; лист 7, записи ИЗ-2, ИЗ-4, ИЗ-5).

Примечания

1. Коды цвета — ориентир подбора по веерам производителей красок; ткань утверждается по образцу при дневном свете и при свете проекта 2700–3000 K.
2. Размеры полотен — по замеру после чистовой отделки пола и потолка; ширина полотна указана с учётом сборки, без припусков на швы. Схемы окон и отметки шин лист 62.
3. Портьеры и тюль — на тесьме «волна» по системе шины; блэкаут — подкладкой. Ковры — на противоскользящей подложке.
4. Замена изделия — аналогом по характеристикам (состав, плотность, размер, цвет по образцу) с согласованием автора проекта.
5. Места изделий — план текстиля и декора (лист 61); подушки и пледы — по марке мебели.

Изм.	Кол.уч	Лист	№ док.	Подп.	Дата
Разраб.		Кырлан А.С.			14.11.26
Пров.					
ГИП					
Н. контр.					
Утв.					

ГД-2026-006-АИ

Квартира 58 м²

Общая площадь 55,23* м² · * размеры приняты, не замерены (реестр — л. 6, 7, К-5)

Дизайн-проект интерьера

Стадия	Лист	Листов
РП	63	108

Ведомость текстиля

М б/м

Кырлан Александр Сергеевич

Ведомость декора. Схемы развески

ПРЕДВАРИТЕЛЬНО · не для производства работ · открыто пунктов: 9 (реестр — л. 6, 7)


Картины, зеркала, растения, настольный декор · схемы развески (М 1:50) · высоты — мм от чистого пола

Декор: картины, зеркала, растения, предметы


картина · зеркало · мебель под изделием

Поз.	Пом.	Предмет	Размер, мм	Место: стена, высота от пола, мм	Масса, кг	Крепёж и основание	Свет места, отделка	Кол.
ДК1**	1	Постер над диваном, левый: Линия берега и два камня, тушь	600×800	стена Б, привязка 1460; низ 1050, центр 1450; над М1**	3	дюбель с крюком, 2 точки; основание: бетон; нагрузка 10 кг	рама — дуб	1
ДК2**	1	Постер над диваном, правый: Три мягких пятна пыльный синий, шалфей, песок, гуашь	600×800	стена Б, привязка 2140; низ 1050, центр 1450; над М1**	3	дюбель с крюком, 2 точки; основание: бетон; нагрузка 10 кг	рама — дуб	1
ДК3**	1	Фикус каучуконосный в напольном керамическом кашпо Ø400, матовый белый	450×450	напольное			свет средний	1
ДК4**	1	Ваза керамическая с веткой эвкалипта на обеденном столе, матовая глазурь, пыльный синий	200×300	на М3 (обеденный стол)			NCS S 4010-R90B (пыльный синий)	1
ДК5**	2	Картина над кроватью: Туманный фьорд на рассвете, акварель	1100×700	стена Б, привязка 1550; низ 1200, центр 1550; над С1	4	дюбель с крюком, 2 точки; основание: перегородка — определить обмером до монтажа; нагрузка 10 кг	рама — дуб	1
ДК6**	2	Зеркало в рост в тонкой дубовой раме 600×1600	600×1600	стена В, привязка 1440; низ 300, центр 1100	12	анкер для пустотелых оснований, 4 шт.; основание: перегородка — определить обмером до монтажа; нагрузка 30 кг	рама — дуб	1
ДК7**	2	Замиокулькас в напольном кашпо Ø350, керамика	400×400	напольное			свет слабый	1
ДК8**	3	Зеркало над умывальником, влагостойкое, в тонкой дубовой раме 450×650	450×650	стена В, привязка 1600; низ 1150, центр 1475; над П3**	5	клей для зеркал + 2 опорных уголка снизу; основание: стена под керамогранитом — основание — определить обмером до монтажа; нагрузка 15 кг		1
ДК9**	4	Постер в тонкой чёрной раме 300×400: Маяк на шхере, линейный рисунок тушью	300×400	стена В, привязка 900; центр 1500	1	дюбель с крюком, 1 точка; основание: стена под керамогранитом — основание — определить обмером до монтажа; нагрузка 5 кг	рама — чёрный матовый металл	1
ДК10**	5	Зеркало в рост в дубовой раме 600×1700	600×1700	стена А, привязка 440; низ 300, центр 1150	12	анкер для пустотелых оснований, 4 шт.; основание: перегородка — определить обмером до монтажа; нагрузка 30 кг	рама — дуб	1
ДК11**	5	Постер между дверями: Ветка эвкалипта, линогравюра	400×560	стена А, привязка 2690; центр 1500	2	дюбель с крюком, 2 точки; основание: перегородка — определить обмером до монтажа; нагрузка 10 кг	рама — дуб	1
ДК12**	4	Ваза-бутыль керамическая, шалфей, с сухой веткой эвкалипта — на полке короба инсталляции	130×400	напольное			NCS S 3010-G10Y (шалфей средний)	1


ДК1, ДК2** — Кухня-гостиная (пом. 1), стена Б, группа «постеры» (М 1:50)**

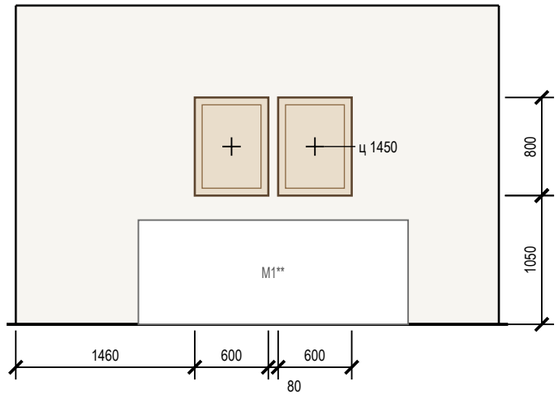


ДК5 — Спальня (пом. 2), стена Б (М 1:50)**

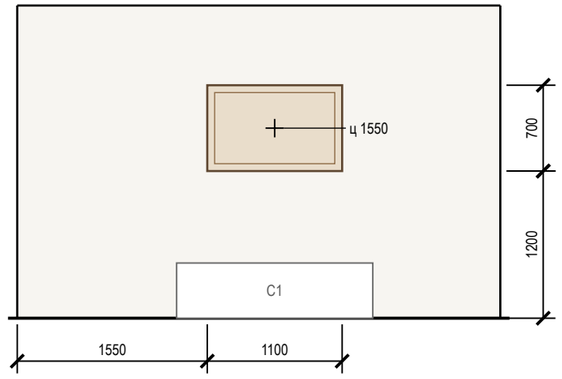

ДК6 — Спальня (пом. 2), стена В (М 1:50)**

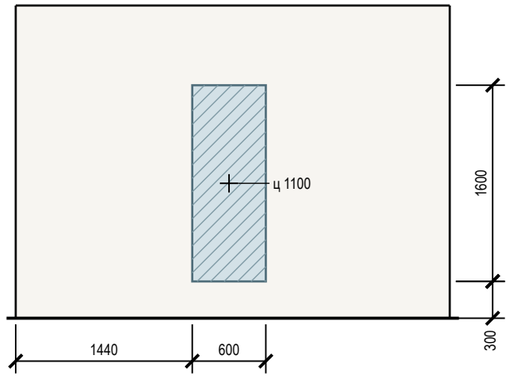

ДК8 — Ванная (пом. 3), стена В (М 1:50)**

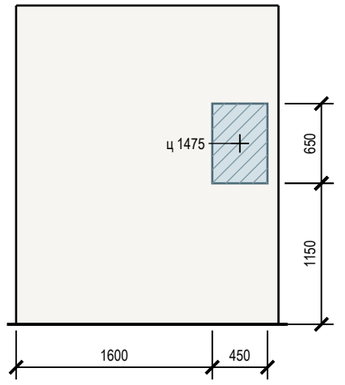

Допущения и предложения на листе

Основа листа: размеры сняты с плана заказчика, контрольный обмер не выполнен (К-5); высота потолка 2700 мм принята: на плане заказчика не указана (К-5); подрайон климата не задан — принят не северный (жилые от 2,5 м) (К-4); толщины стен приняты: наружные 250 мм, перегородки 120 мм — не обмерены (К-5); разрешённая мощность 15 кВт принята по типовой квартире, технических условий нет (К-6).

Знак «**» — предложение проектировщика, заказчиком не утверждено (согласовать с заказчиком): ИЗ-2, ИЗ-4: М1 — Было offset 1300…3500: торец дивана в 500 мм от стены В, правые 350 мм проёма Д-2 (3900…4800) упирались в диван; ИЗ-4: ДК1, ДК2, ДК3, ДК4, ДК5, ДК6, ДК7, ДК8, ДК9, ДК10, ДК11; ИЗ-5: ДК12; К-2: П3 — умывальник у стены В справа от ванны — перед ним свободно 750 мм, до стены Б 90 мм.

Изменения по листу без подписи: ИЗ-4, ИЗ-5.

См. лист открытых вопросов (лист 6, записи К-2, К-4–К-6; лист 7, записи ИЗ-2, ИЗ-4, ИЗ-5).

Примечания

1. Высоты — от чистого пола помещения до низа изделия, «ц» — до центра; привязки — от чистовой грани угла стены, мм.
2. Над мебелью низ изделия — на 150–250 мм выше спинки или изголовья; без мебели центр — на 1450–1600 мм от пола.
3. Изделия до 5 кг — на два подвеса по основанию; тяжелее — на анкеры с нагрузкой не меньше двойной массы; на ГКЛ — только по закладной или анкеру для пустотелых оснований.
4. Зеркала в рост — с креплением от опрокидывания; в санузлах — влагостойкие, на клей для зеркал и нейтральный силикон.
5. Места изделий — план текстиля и декора (лист 61). Схемы развески остальных изделий — лист 65.

Изм.	Кол.уч	Лист	№ док.	Подп.	Дата
Разраб.		Кырлан А.С.			14.11.26
Пров.					
ГИП					
Н. контр.					
Утв.					

ГД-2026-006-АИ

Квартира 58 м²

Общая площадь 55,23* м² · * размеры приняты, не замерены (реестр — л. 6, 7, К-5)

Дизайн-проект интерьера

Стадия	Лист	Листов
РП	64	108

Ведомость декора. Схемы развески

М б/м

Кырлан Александр Сергеевич

выпуск 14.11.2026 № bcee049e32 · стр. 72 из 128

Схемы развески (продолжение)


Схемы развески картин и зеркал (М 1:25) · высоты — мм от чистого пола

ПРЕДВАРИТЕЛЬНО · не для производства работ · открыто пунктов: 9 (реестр — л. 6, 7)


Ведомость декора (размер, масса, крепёж и основание) — лист 64

картина · зеркало · мебель под изделием


ДК9 — Санузел (пом. 4), стена В (М 1:25)**

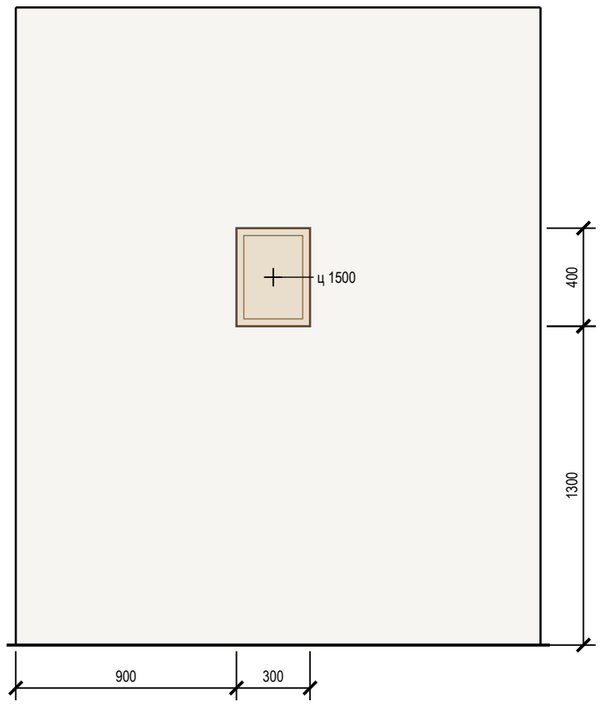

ДК10 — Прихожая (пом. 5), стена А (М 1:25)**

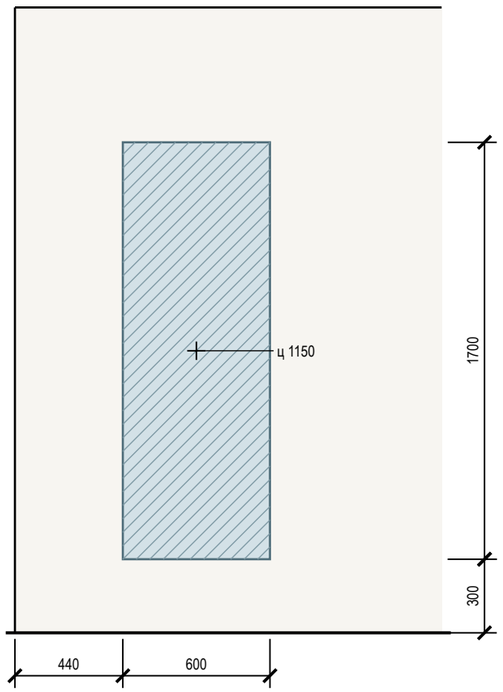

ДК11 — Прихожая (пом. 5), стена А (М 1:25)**

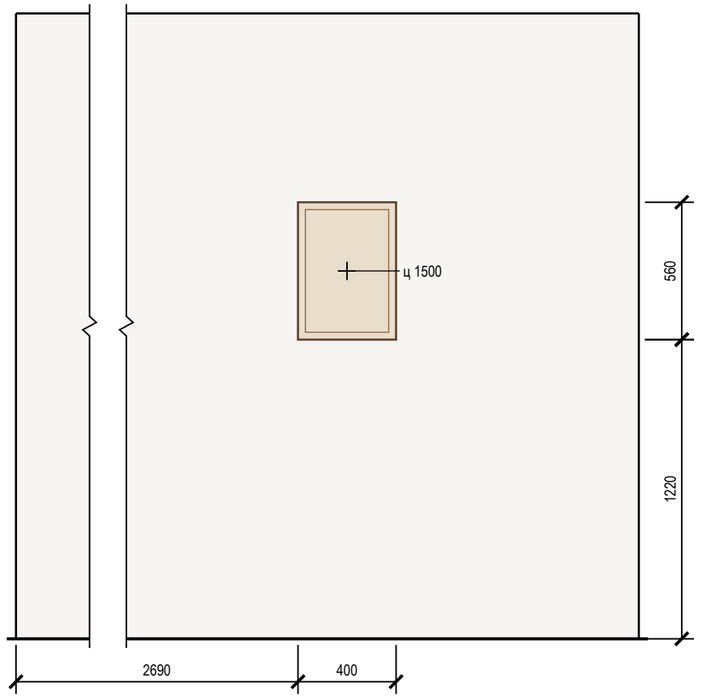

Допущения и предложения на листе

Основа листа: размеры сняты с плана заказчика, контрольный обмер не выполнен (К-5); высота потолка 2700 мм принята: на плане заказчика не указана (К-5); подрайон климата не задан — принят не северный (жилые от 2,5 м) (К-4); толщины стен приняты: наружные 250 мм, перегородки 120 мм — не обмерены (К-5); разрешённая мощность 15 кВт принята по типовой квартире, технических условий нет (К-6).

Знак «**» — предложение проектировщика, заказчиком не утверждено (согласовать с заказчиком): ИЗ-4: ДК9, ДК10, ДК11.

См. лист открытых вопросов (лист 6, записи К-4–К-6; лист 7, запись ИЗ-4).

Примечания

1. Высоты — от чистого пола помещения до низа изделия, «ц» — до центра; привязки — от чистовой грани угла стены, мм.
2. Над мебелью низ изделия — на 150–250 мм выше спинки или изголовья; без мебели центр — на 1450–1600 мм от пола.
3. Изделия до 5 кг — на два подвеса по основанию; тяжелее — на анкеры с нагрузкой не меньше двойной массы; на ГКЛ — только по закладной или анкеру для пустотелых оснований.
4. Зеркала в рост — с креплением от опрокидывания; в санузлах — влагостойкие, на клей для зеркал и нейтральный силикон.
5. Места изделий — план текстиля и декора (лист 61). Ведомость декора: размер, масса, крепёж и основание — лист 64.

Изм.	Кол.уч	Лист	№ док.	Подп.	Дата
Разраб.		Кырлан А.С.			14.11.26
Пров.					
ГИП					
Н. контр.					
Утв.					

ГД-2026-006-АИ

Квартира 58 м²

Общая площадь 55,23* м² · * размеры приняты, не замерены (реестр — л. 6, 7, К-5)

Дизайн-проект интерьера

Стадия	Лист	Листов
РП	65	108

Схемы развески (продолжение)

М б/м


Кырлан Александр Сергеевич

выпуск 14.11.2026 № bcee049e32 · стр. 73 из 128

Встроенная мебель. Схема расположения

встроенная и корпусная мебель на заказ, кухонный гарнитур · размеры в мм · марки — по ведомости изделий

ПРЕДВАРИТЕЛЬНО · не для производства работ · открыто пунктов: 9 (реестр — л. 6, 7)

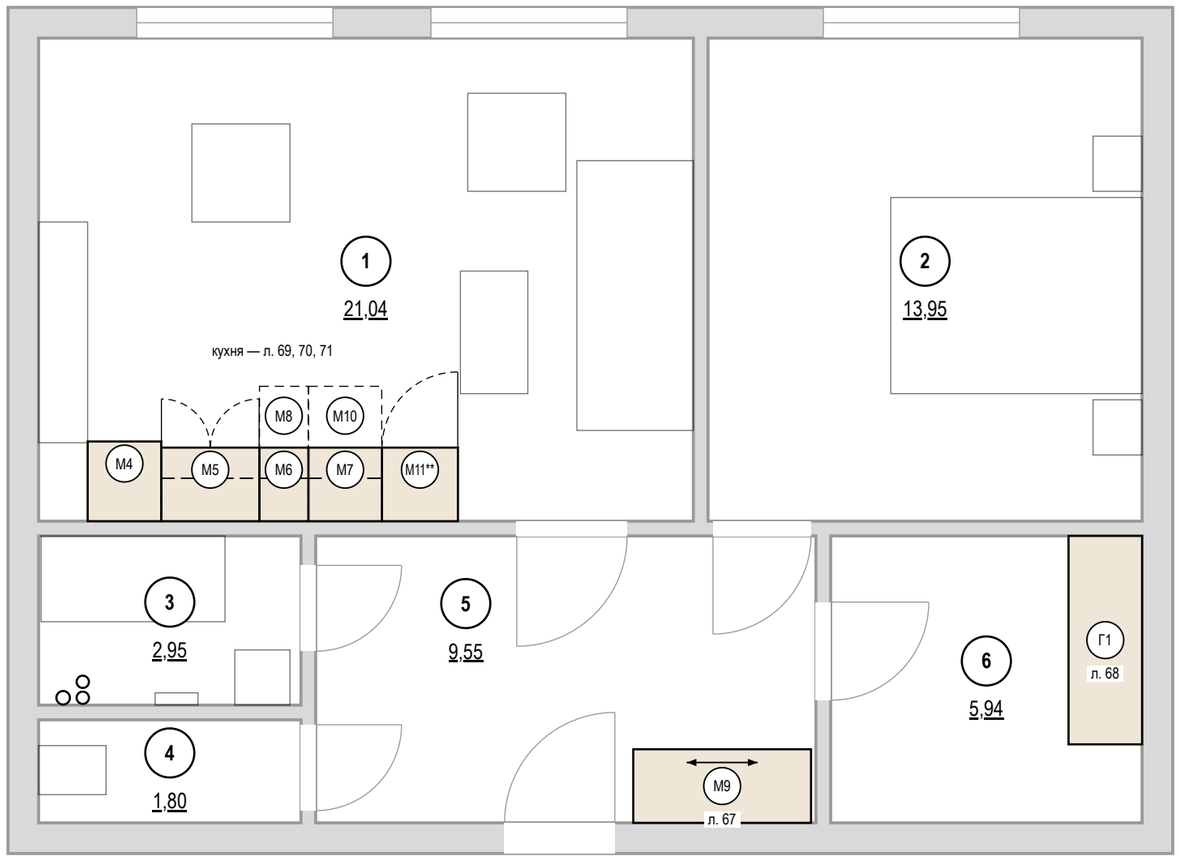

Ведомость изделий

Марка	Наименование	Пом.	Ш×Г×В, мм	Лист
M9	Шкаф-купе	5	1450×600×2450	67
Г1	Система хранения	6	1700×600×2400	68
M11**	Ниша под стиральную машину 620: без корпуса, между боковинами соседних модулей, фасад на петлях к боковине соседнего модуля; цоколь съёмный	1	620×600×900	69, 70
M7	Модуль нижний: ящики, варочная	1	600×600×900	69, 70
M10	Модуль навесной: полки	1	600×350×620	69, 70
M6	Модуль нижний: ящики	1	400×600×900	69, 70
M8	Модуль навесной: полки, сушка	1	1200×350×720	69, 70
M5	Модуль нижний: мойка	1	800×600×900	69, 70
M4	Место под холодильник отдельностоящий: без корпуса и фасада	1	600×650×2100	69, 70

Условные обозначения

- изделие мебельщика: корпус на полу
- невидимый контур: навесной модуль, корпус под столешницей
- открывание распашного фасада
- зона выдвижения ящика, двери техники
- дверь купе, стрелка — направление движения
- K1 — марка изделия или модуля (на схеме расположения под ней — лист изделия)

Допущения и предложения на листе

Основа листа: размеры сняты с плана заказчика, контрольный обмер не выполнен (К-5); высота потолка 2700 мм принята: на плане заказчика не указана (К-5); подрайон климата не задан — принят не северный (жилые от 2,5 м) (К-4); толщины стен приняты: наружные 250 мм, перегородки 120 мм — не обмерены (К-5); разрешённая мощность 15 кВт принята по типовой квартире, технических условий нет (К-6).

Знак «**» — предложение проектировщика, заказчиком не утверждено (согласовать с заказчиком): К-7: M11 — место стиральной машины: вместо модуля с ящиками 400 справа от варочной; ряд до 3420, журнальный стол M21 (с х 3440) не мешает загрузке.

См. лист открытых вопросов (лист 6, записи К-4–К-7).

Примечания

1. Изделия — по чистовым размерам помещений; перед раскроем — контрольный замер цеха после чистовой отделки стен, пола и потолка.
2. Открывание фасадов и выдвижение ящиков показано в открытом положении: зоны не пересекают двери, радиаторы, выключатели и проходы.
3. Стояки и счётчики за мебелью — с сервисным люком; газовые трубы мебелью не зашиваются.
4. Покупная мебель — по плану расстановки мебели и спецификации дизайнера; здесь — подложкой.

1000 мм · печать 1:1

Изм.	Кол.уч	Лист	№ док.	Подп.	Дата				
Разраб.		Кырлан А.С.			14.11.26	**ГД-2026-006-АИ**			
Пров.						Квартира 58 м²			
ГИП						Общая площадь 55,23* м² · * размеры приняты, не замерены (реестр — л. 6, 7, К-5)			
						Дизайн-проект интерьера	Стадия	Лист	Листов
Н. контр.							РП	66	108
Утв.						**Встроенная мебель. Схема расположения** М 1:50	**Кырлан Александр Сергеевич**		


выпуск 14.11.2026 № bcee049e32 · стр. 74 из 128

Шкаф-купе М9


Прихожая (пом. 5) · вид из помещения · размеры в мм, отметки в м

ПРЕДВАРИТЕЛЬНО · не для производства работ · открыто пунктов: 9 (реестр — л. 6, 7)


Вид с фасадами (М 1:20)

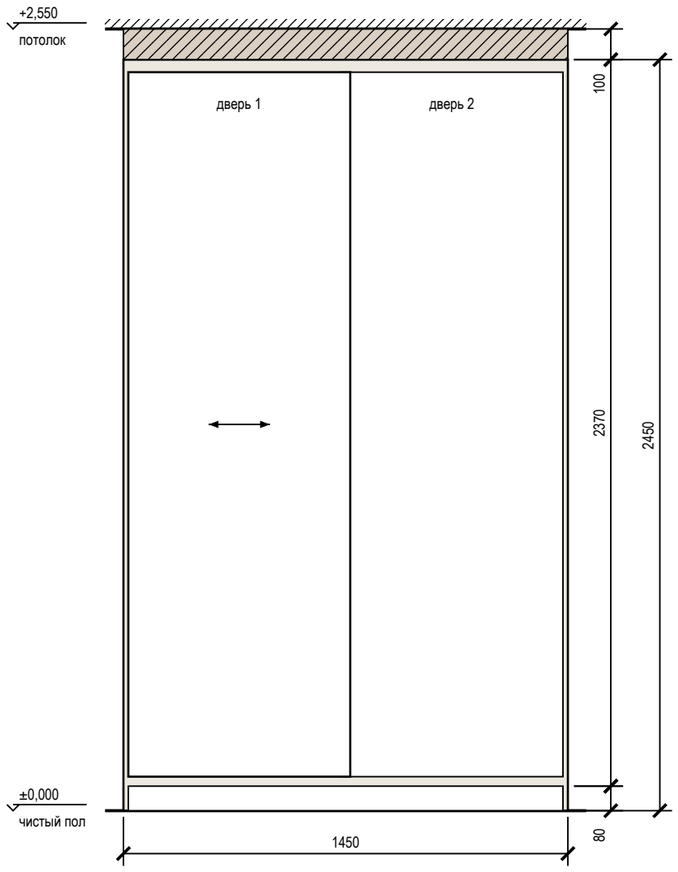


Вид без фасадов (М 1:20)

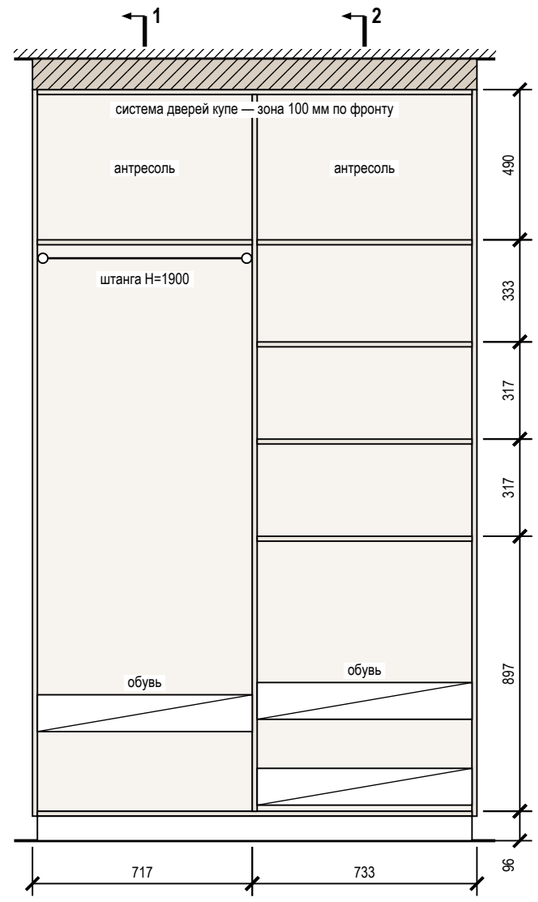

Разрез 1-1 (М 1:20)

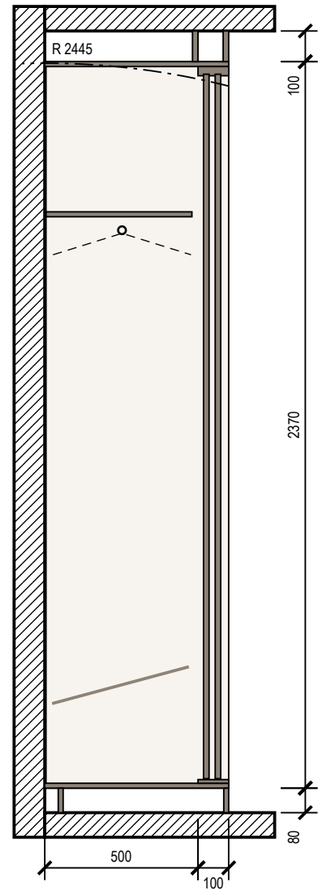

Разрез 2-2 (М 1:20)

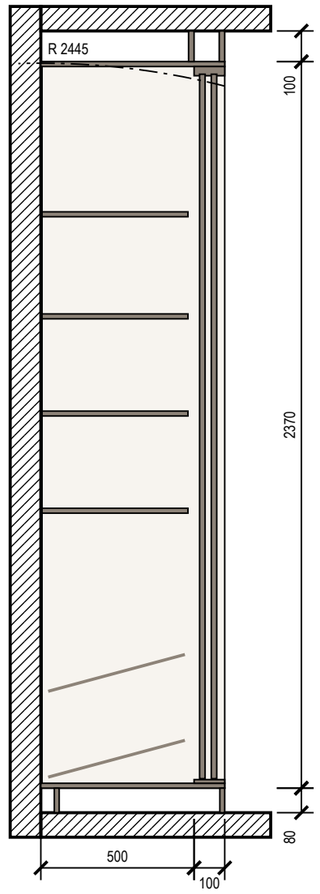

Примечания

1. Размеры — в мм по чистовой отделке; изделие 1450×600×2450 (Ш×Г×В). Перед раскроем — контрольный замер цеха после чистовой отделки стен, пола и потолка.
2. Корпус — ЛДСП 16 мм, задняя стенка ХДФ 4 мм в паз, цоколь 80 мм на регулируемых опорах; двери купе — ЛДСП 10 мм в алюминиевом профиле; нахлёст 30 мм, ширина двери 724 мм, высота — проём минус 40 мм; цвет — по колерной карте.
3. Кромка: скрытые торцы 0,4 мм, видимые 1 мм (ПВХ/АБС).
4. Номинальные зазоры: дверь купе — боковина 3 мм, фасад ящика — стойка 2 мм; ящики внутри купе — с накладкой 30 мм на стойке со стороны нахлёста дверей.
5. Присадка по 32-й системе — выполняет цех.
6. Компенсатор 100 мм — короб из ЛДСП по фронту и торцам, подгоняется к потолку при монтаже (припуск 20 мм), крепится к корпусу и к потолку.
7. Подъём корпуса: диагональ боковины без цоколя $\sqrt{(2370^2 + 600^2)} = 2445$ мм < 2550 мм до потолка — корпус собирается лёжа, поднимается поворотом и ставится на цоколь.
8. Крепление к стене от опрокидывания — уголки 2 шт. к несущему основанию (монтажная схема шкафов).

Условные обозначения

- дверь купе, стрелка — направление движения
- корпус и полки ЛДСП (вид на стену)
- задняя стенка ХДФ
- деталь в разрезе
- компенсатор — короб до потолка
- штанга для плечиков (на разрезе — плечики 450 мм)
- траектория угла корпуса при подъёме в проектное положение

Допущения и предложения на листе

Основа листа: размеры сняты с плана заказчика, контрольный обмер не выполнен (К-5); высота потолка 2700 мм принята: на плане заказчика не указана (К-5); подрайон климата не задан — принят не северный (жилые от 2,5 м) (К-4); толщины стен приняты: наружные 250 мм, перегородки 120 мм — не обмерены (К-5); разрешённая мощность 15 кВт принята по типовой квартире, технических условий нет (К-6).

См. лист открытых вопросов (лист 6, записи К-4–К-6).

1000 мм · печать 1:1

Изм.	Кол.уч	Лист	№ док.	Подп.	Дата
Разраб.		Кырлан А.С.			14.11.26
Пров.					
ГИП					
Н. контр.					
Утв.					

ГД-2026-006-АИ

Квартира 58 м²

Общая площадь 55,23* м² · * размеры приняты, не замерены (реестр — л. 6, 7, К-5)

Дизайн-проект интерьера

Стадия	Лист	Листов
РП	67	108

Шкаф-купе М9

М 1:20

Кырлан Александр Сергеевич


выпуск 14.11.2026 № bcee049e32 · стр. 75 из 128

Система хранения Г1


Гардеробная (пом. 6) · вид из помещения · размеры в мм, отметки в м

ПРЕДВАРИТЕЛЬНО · не для производства работ · открыто пунктов: 9 (реестр — л. 6, 7)


Общий вид (М 1:20)

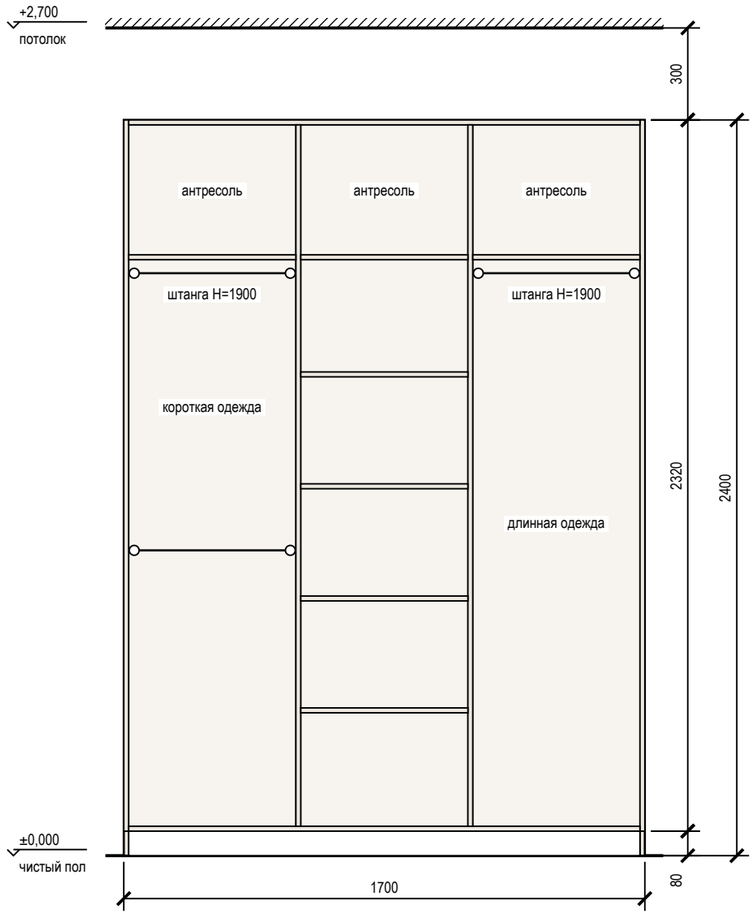


Наполнение, размеры в свету (М 1:20)

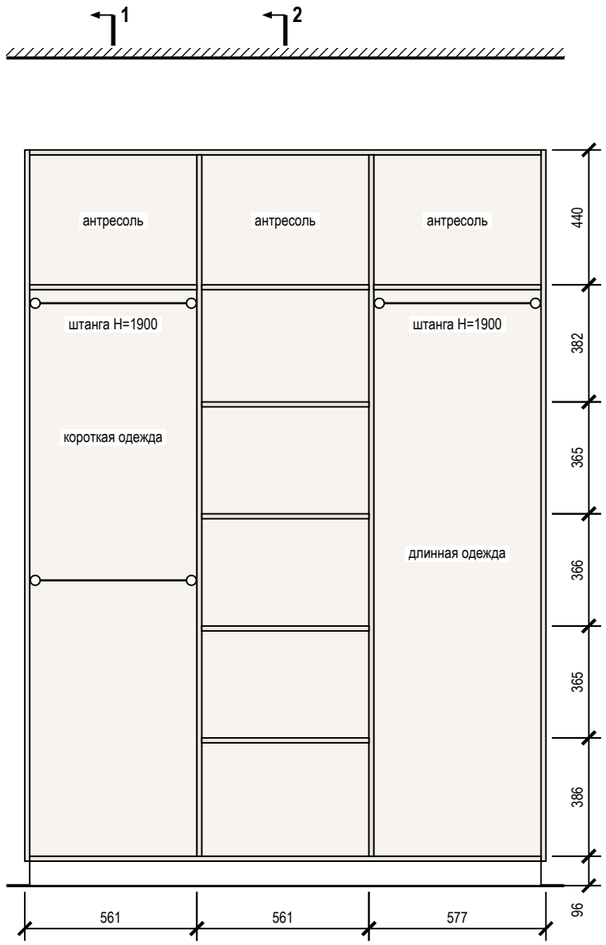

Разрез 1-1 (М 1:20)

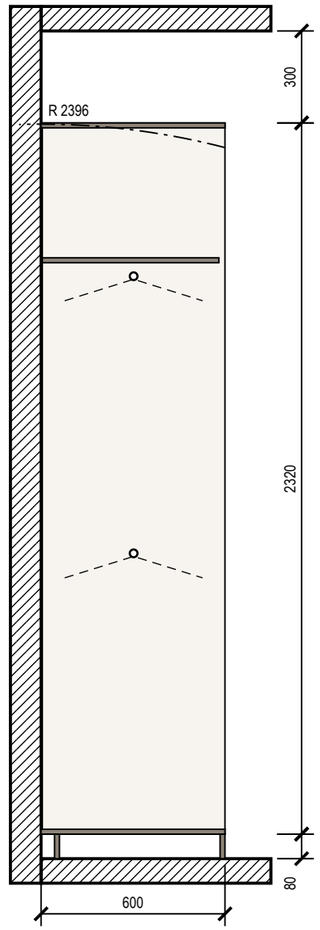

Разрез 2-2 (М 1:20)

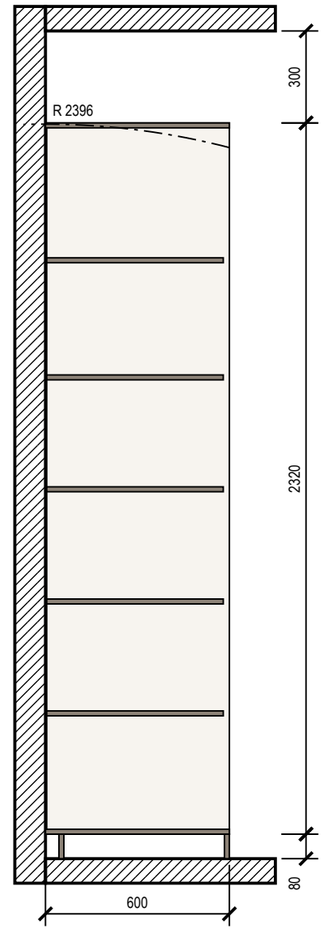

Примечания

1. Размеры — в мм по чистовой отделке; изделие 1700×600×2400 (Ш×Г×В). Перед раскроем — контрольный замер цеха после чистовой отделки стен, пола и потолка.
2. Корпус — ЛДСП 16 мм, задняя стенка ХДФ 4 мм в паз, цоколь 80 мм на регулируемых опорах; открытая система: без фасадов.
3. Кромка: скрытые торцы 0,4 мм, видимые 2 мм (ПВХ/АБС).
4. Присадка по 32-й системе — выполняет цех.
5. Зазор до потолка 300 мм.
6. Подъём корпуса: диагональ боковины без цоколя √(2320² + 600²) = 2396 мм < 2700 мм до потолка — корпус собирается лёжа, поднимается поворотом и ставится на цоколь.
7. Крепление к стене от опрокидывания: крепление к стене, 3 точки; основание стены и шаг анкеров — монтажная схема шкафов.

Условные обозначения

- корпус и полки ЛДСП (вид на стену)
- задняя стенка ХДФ
- деталь в разрезе
- штанга для плечиков (на разрезе — плечики 450 мм)
- траектория угла корпуса при подъёме в проектное положение

Допущения и предложения на листе

Основа листа: размеры сняты с плана заказчика, контрольный обмер не выполнен (К-5); высота потолка 2700 мм принята: на плане заказчика не указана (К-5); подрайон климата не задан — принят не северный (жилые от 2,5 м) (К-4); толщины стен приняты: наружные 250 мм, перегородки 120 мм — не обмерены (К-5); разрешённая мощность 15 кВт принята по типовой квартире, технических условий нет (К-6).

См. лист открытых вопросов (лист 6, записи К-4–К-6).

1000 мм · печать 1:1

Изм.	Кол.уч	Лист	№ док.	Подп.	Дата
Разраб.		Кырлан А.С.			14.11.26
Пров.					
ГИП					
Н. контр.					
Утв.					

ГД-2026-006-АИ

Квартира 58 м²

Общая площадь 55,23* м² · * размеры приняты, не замерены (реестр — л. 6, 7, К-5)

Дизайн-проект интерьера

Стадия	Лист	Листов
РП	68	108

Система хранения Г1

М 1:20


Кырлан Александр Сергеевич

выпуск 14.11.2026 № bcee049e32 · стр. 76 из 128

Кухня (пом. 1). Развёртка гарнитура

Кухня-гостиная (пом. 1) · стена В · вид из помещения · размеры в мм, отметки в м · лист 1: вид с фасадами

Вид с фасадами (М 1:20)

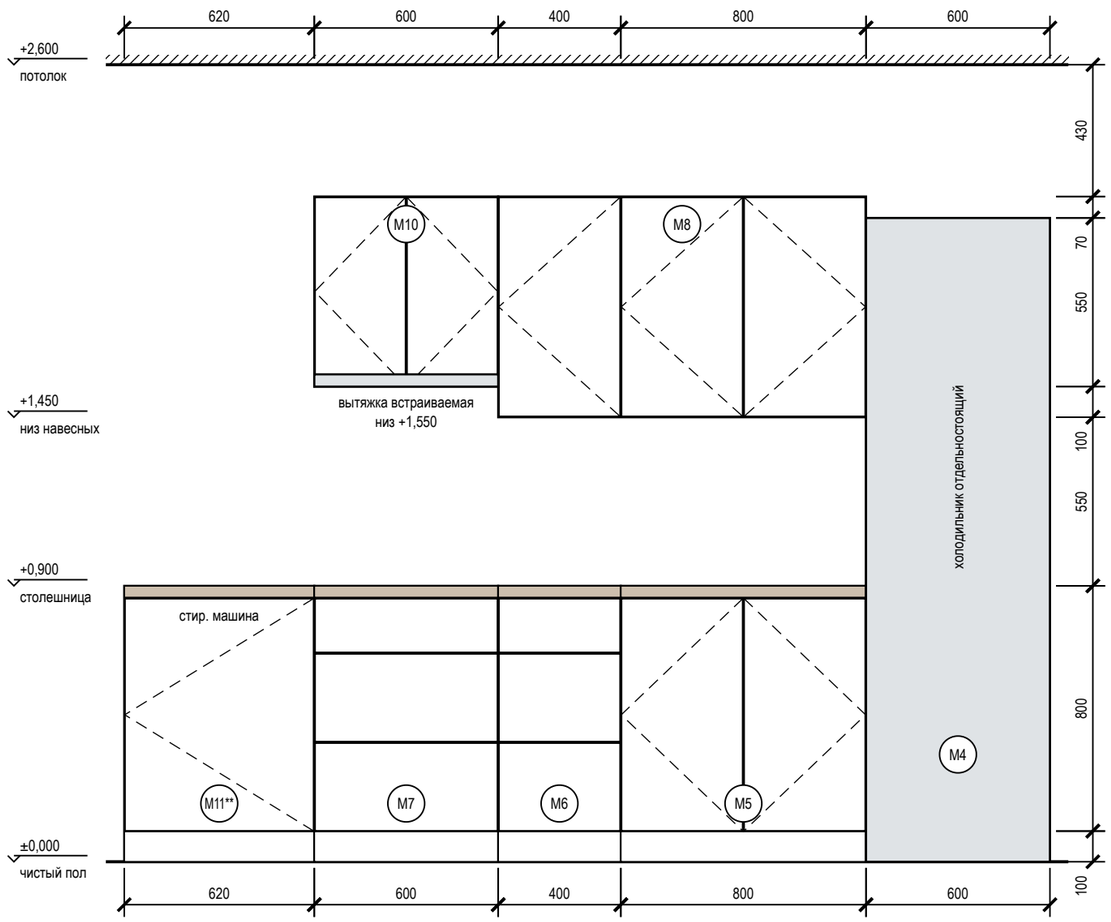

Условные обозначения

- фасад распашной: линии сходятся к стороне петель
- фасад ящика, карго
- встраиваемая техника
- столешница
- доборная планка
- деталь в разрезе
- (K1) марка изделия или модуля (на схеме расположения под ней — лист изделия)
- розетка на стене
- вывод кабеля к технике
- В1 вывод воды В1 / Т3, канализации К1

Примечания

1. Размеры — в мм по чистовой отделке, вид из помещения; марки — как на плане расстановки. Перед раскроем — контрольный замер цеха после фартука и пола.
2. Корпуса — ЛДСП 16 мм, задняя стенка ХДФ 4 мм; фасады — МДФ эмаль 18 мм, цвет по колерной карте; столешница 38 мм, свес 20 мм; цоколь 100 мм.
3. Кромка: скрытые торцы 0,4 мм, видимые 1 мм. Номинальные зазоры: между фасадами 3 мм, фасад — столешница 3 мм, фасад — стена не менее 3 мм.
4. Ящики полного выдвижения и петли — с доводчиком; присадка по 32-й системе — выполняет цех.

Ведомость модулей

Мод.	Наименование	Ш×Г×В, мм	Низ, мм
M11**	Ниша под стиральную машину 620: без корпуса, между боковинами соседних модулей, фасад на петлях к боковине соседнего модуля; цоколь съёмный	620×600×900	от цоколя
M7	Модуль нижний: ящики, варочная	600×600×900	от цоколя
M6	Модуль нижний: ящики	400×600×900	от цоколя
M5	Модуль нижний: мойка	800×600×900	от цоколя

Мод.	Наименование	Ш×Г×В, мм	Низ, мм
M10	Модуль навесной: полки	600×350×620	+1550
M8	Модуль навесной: полки, сушка	1200×350×720	+1450
M4	Место под холодильник отдельностоящий: без корпуса и фасада	600×650×2100	от пола

Допущения и предложения на листе

Основа листа: размеры сняты с плана заказчика, контрольный обмер не выполнен (К-5); высота потолка 2700 мм принята: на плане заказчика не указана (К-5); подрайон климата не задан — принят не северный (жилые от 2,5 м) (К-4); толщины стен приняты: наружные 250 мм, перегородки 120 мм — не обмерены (К-5); разрешённая мощность 15 кВт принята по типовой квартире, технических условий нет (К-6).

Знак «**» — предложение проектировщика, заказчиком не утверждено (согласовать с заказчиком): К-7: M11 — место стиральной машины: вместо модуля с ящиками 400 справа от варочной; ряд до 3420, журнальный стол M21 (с x 3440) не мешает загрузке.

См. лист открытых вопросов (лист 6, записи К-4–К-7).

1000 мм · печать 1:1

Изм.	Кол.уч	Лист	№ док.	Подп.	Дата
Разраб.		Кырлан А.С.			14.11.26
Пров.					
ГИП					
Н. контр.					
Утв.					

ГД-2026-006-АИ

Квартира 58 м²

Общая площадь 55,23* м² · * размеры приняты, не замерены (реестр — л. 6, 7, К-5)

Дизайн-проект интерьера

Стадия	Лист	Листов
РП	69	108

Кухня (пом. 1). Развёртка гарнитура

М 1:20

Кырлан Александр Сергеевич


выпуск 14.11.2026 № bcee049e32 · стр. 77 из 128

Кухня (пом. 1). Развёртка гарнитура: вид без фасадов и разрезы


Кухня-гостиная (пом. 1) · стена В · вид из помещения · размеры в мм, отметки в м · лист 2: вид без фасадов, разрезы

ПРЕДВАРИТЕЛЬНО · не для производства работ · открыто пунктов: 9 (реестр — л. 6, 7)


Вид без фасадов: наполнение, выводы (М 1:20)

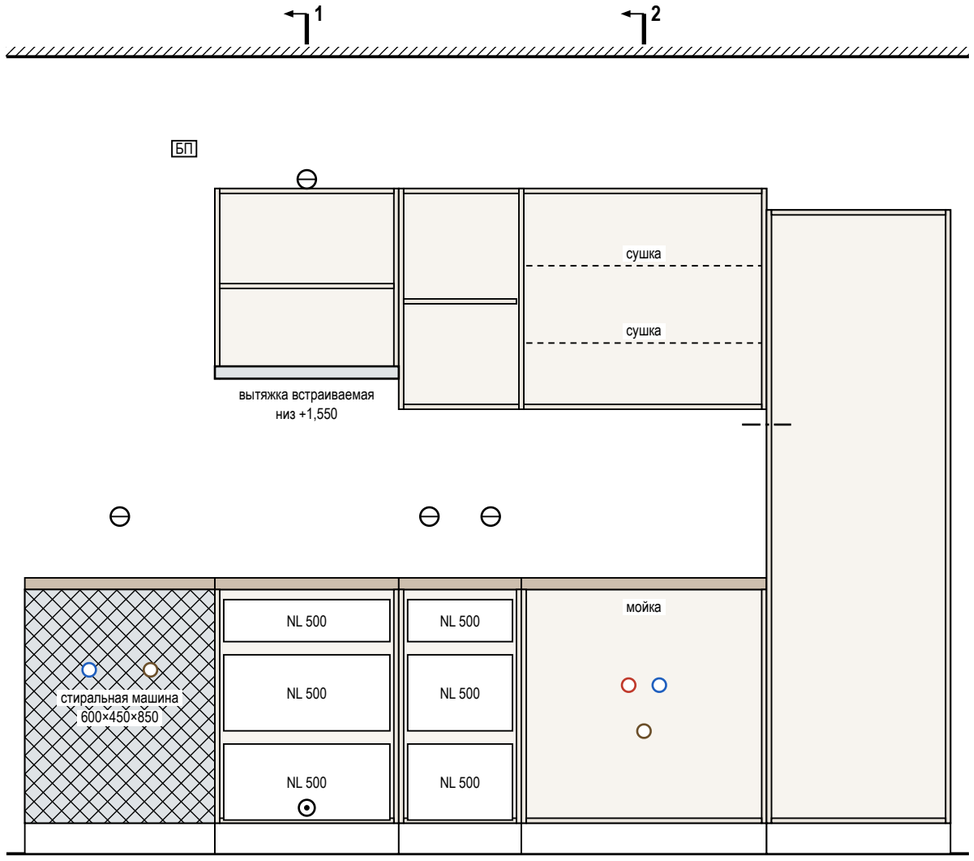

Разрез 1-1 (М 1:20)

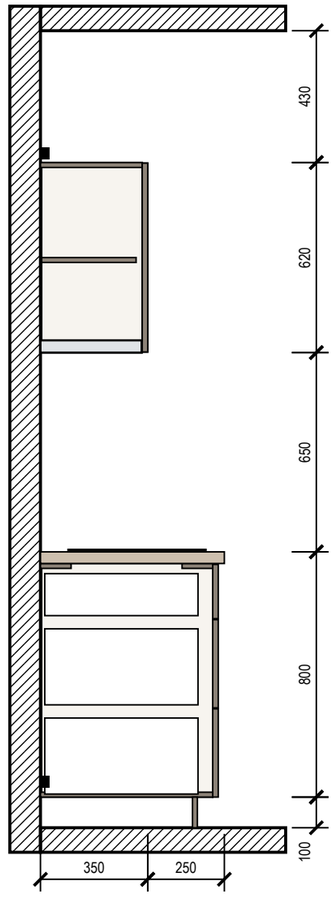

Разрез 2-2 (М 1:20)

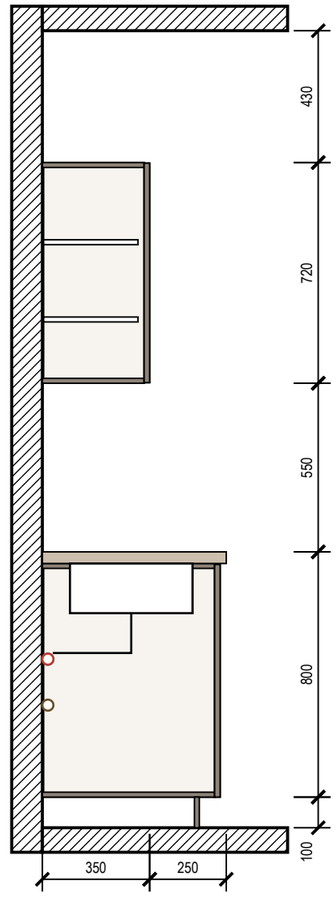

Примечания

1. Вытяжка встраивается в дно навесного модуля М10 над варочной: её низ на 1550 мм от пола, 650 мм над панелью (не меньше 650 мм).
2. Ниши техники — по монтажным схемам выбранных моделей: решётка в цоколе и канал за пеналом холодильника, зазор за духовым шкафом, фасад ПММ на двери машины.

Допущения и предложения на листе

Основа листа: размеры сняты с плана заказчика, контрольный обмер не выполнен (К-5); высота потолка 2700 мм принята: на плане заказчика не указана (К-5); подрайон климата не задан — принят не северный (жилые от 2,5 м) (К-4); толщины стен приняты: наружные 250 мм, перегородки 120 мм — не обмерены (К-5); разрешённая мощность 15 кВт принята по типовой квартире, технических условий нет (К-6).

См. лист открытых вопросов (лист 6, записи К-4–К-6).

1000 мм · печать 1:1

Изм.	Кол.уч	Лист	№ док.	Подп.	Дата
Разраб.		Кырлан А.С.			14.11.26
Пров.					
ГИП					
Н. контр.					
Утв.					

ГД-2026-006-АИ

Квартира 58 м²

Общая площадь 55,23* м² · * размеры приняты, не замерены (реестр — л. 6, 7, К-5)

Дизайн-проект интерьера

Стадия	Лист	Листов
РП	70	108

Кухня (пом. 1). Развёртка гарнитура: вид без фасадов и разрезы

М 1:20

Кырлан Александр Сергеевич


выпуск 14.11.2026 № bcee049e32 · стр. 78 из 128

Кухня (пом. 1). Монтажная схема


Кухня-гостиная (пом. 1) · стена В · размеры в мм от чистых поверхностей, высоты — от чистого пола

ПРЕДВАРИТЕЛЬНО · не для производства работ · открыто пунктов: 9 (реестр — л. 6, 7)

Привязка выводов и крепление модулей (М 1:20)

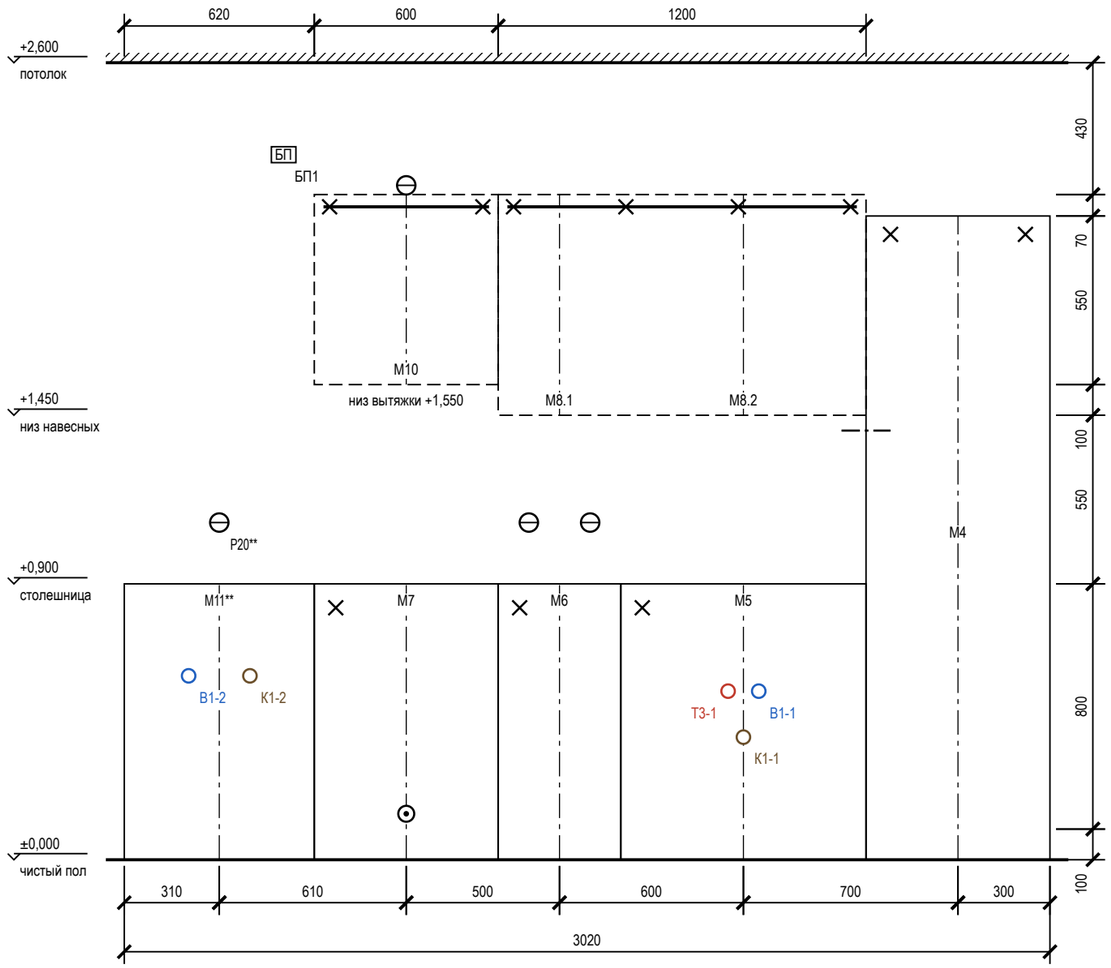

План столешницы (М 1:20)

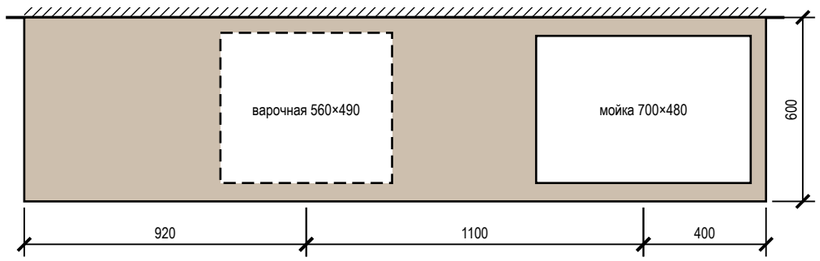

Привязка выводов к осям модулей

Код	Назначение	Модуль	От оси, мм	Н, мм	Размещение
В1-2	В1 — кран машины	М11**	−100	600	в нише стиральной машины, за машиной (доступ — выдвинуть машину)
Р20**	розетка — стиральная машина	М11**	0	1100	над столешницей (фартук)
К1-2	К1 Ø40 — стиральная машина	М11**	+100	600	в нише стиральной машины, за машиной (доступ — выдвинуть машину)
БП1	блок питания	М11**	+210	2300	над столешницей (фартук)
	вывод кабеля — варочная панель	М7	0	150	в соседнем модуле, за ящиком
	розетка — вытяжка (встроена в дно М10)	М10	0	2200	в навесном модуле
	розетка — рабочая зона	М6	−100	1100	над столешницей (фартук)
	розетка ×2 — рабочая зона	М6	+100	1100	над столешницей (фартук)
Т3-1	Т3** — межос. 100	М5	−50	550	в модуле мойки
К1-1	К1 Ø50 — мойка	М5	0	400	в модуле мойки
В1-1	В1 — межос. 100	М5	+50	550	в модуле мойки
	светодиодная лента — подсветка столешницы	М4	−300	1400	за пеналом

Зазоры под отделку

Поверхность	Отделка	Зазор, мм	Учесть
фартук	плитка / стеновая панель	10	от чернового основания до корпуса навесных и столешницы
стены	окраска	5	под штукатурку и шпаклёвку за пеналом
пол	инженерная доска		цоколь — после укладки пола, опоры ±20 мм

Условные обозначения

- нижний модуль, пенал (контур)
- невидимый контур: навесной модуль, корпус под столешницей
- ось модуля (от неё — привязка вывода)
- анкер / уголок крепления к стене
- розетка на стене
- вывод кабеля к технике
- В1 — вывод воды В1 / Т3, канализации К1

Допущения и предложения на листе

Основа листа: размеры сняты с плана заказчика, контрольный обмер не выполнен (К-5); высота потолка 2700 мм принята: на плане заказчика не указана (К-5); подрайон климата не задан — принят не северный (жилые от 2,5 м) (К-4); толщины стен приняты: наружные 250 мм, перегородки 120 мм — не обмерены (К-5); разрешённая мощность 15 кВт принята по типовой квартире, технических условий нет (К-6).

Знак «**» — предложение проектировщика, заказчиком не утверждено (согласовать с заказчиком): ИЗ-4: Т3; К-7: М11 — место стиральной машины: вместо модуля с ящиками 400 справа от варочной; ряд до 3420, журнальный стол М21 (с х 3440) не мешает загрузке; Р20 — питание стиральной машины П6 — отдельная группа 6 (УЗО 30 мА); над столешницей в габарите машины, не за корпусом.

См. лист открытых вопросов (лист 6, записи К-4–К-7; лист 7, запись ИЗ-4).

Примечания

1. Выводы — по проекту электрики и ВК; привязка по горизонтали — от оси модуля (плюс — вправо по виду), по высоте — от чистого пола до оси вывода.
2. Пенал — уголки к стене 2 шт. сверху; нижние модули — стяжками между собой и уголком к стене; ряд выставить по уровню опорами цоколя.
3. Розетки над столешницей — не ниже 150 мм над ней и не за корпусом техники; розетка за ПММ, духовым шкафом и холодильником — только в соседнем модуле или в зоне цоколя с доступом.
4. Столешница — вырезы по шаблонам выбранных моделей мойки и варочной панели; торцы у стены — герметик, пристеночный плинтус.

1000 мм · печать 1:1

Изм.	Кол.уч	Лист	№ док.	Подп.	Дата
Разраб.		Кырлан А.С.			14.11.26
Пров.					
ГИП					
Н. контр.					
Утв.					

ГД-2026-006-АИ

Квартира 58 м²

Общая площадь 55,23* м² · * размеры приняты, не замерены (реестр — л. 6, 7, К-5)

Дизайн-проект интерьера

Стадия	Лист	Листов
РП	71	108

Кухня (пом. 1). Монтажная схема

М 1:20

Кырлан Александр Сергеевич


выпуск 14.11.2026 · bcee049e32 · стр. 79 из 128

Кухня (пом. 1). Столешница: план

Кухня-гостиная (пом. 1) · размеры в мм · вид сверху

План столешницы (вид сверху, стена вверху) М 1:20

Ст-1: стена С, 2420×600

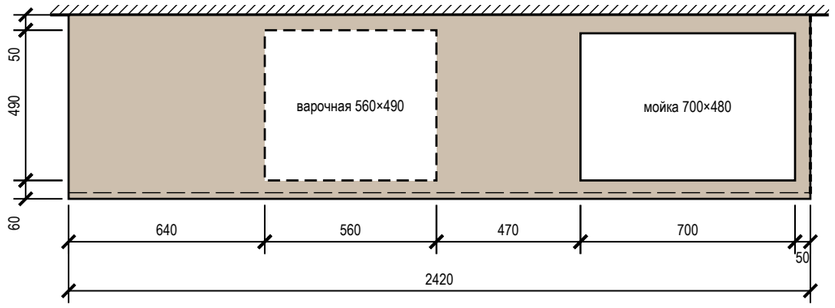

свес над фасадами 20 мм · толщина 38 мм*

Ведомость столешниц

Марка	Стена	Д×Ш×Т, мм	Материал	Вырезы	Кромка	Стыки
Ст-1	С	2420×600×38*	материал не задан (materials.worktop.mat	варочная 560×490; мойка 700×480	3,02 пог. м	нет
Итого			**S = 1,45 м²**		**3,02 пог. м**	

Примечания

1. Материал: материал не задан (materials.worktop.mat) (materials.worktop.mat в данных не задан); толщина 38 мм*.
2. * — толщина принята по практике (38 мм): в данных изделия materials.worktop.thk не задана.
3. Розеток в столешнице нет: питание над столешницей — на фартуке (план розеток), не за корпусом техники.
4. Вырезы: мойка — по габариту чаши 700×480 (прибор), отступ от стены 60 мм; варочная панель — ориентир 560×490 мм, отступ от стены 50 мм; вырезы разметить по шаблону выбранных моделей, углы выреза — радиус не менее 5 мм.
5. Радиусы углов и фаска кромки в данных не заданы: углы столешницы прямые, кромка — прямая без фаски, пока не задано иное.
6. Стыков нет: каждая столешница — одной деталью.
7. Свес над фасадами — 20 мм; торцы: свободный торец — кромка, торец у стены или пенала — зазор не более 3 мм, герметик. Длина кромки — по лицевой стороне и свободным торцам.

Допущения и предложения на листе

Основа листа: размеры сняты с плана заказчика, контрольный обмер не выполнен (К-5); высота потолка 2700 мм принята: на плане заказчика не указана (К-5); подрайон климата не задан — принят не северный (жилые от 2,5 м) (К-4); толщины стен приняты: наружные 250 мм, перегородки 120 мм — не обмерены (К-5); разрешённая мощность 15 кВт принята по типовой квартире, технических условий нет (К-6).

См. лист открытых вопросов (лист 6, записи К-4–К-6).

1000 мм · печать 1:1


						ГД-2026-006-АИ	
						Квартира 58 м²	
Изм.	Кол.уч	Лист	№ док.	Подп.	Дата	Общая площадь 55,23* м² · * размеры приняты, не замерены (реестр — л. 6, 7, К-5)	
Разраб.		Кырлан А.С.			14.11.26	Дизайн-проект интерьера	Стадия: РП; Лист: 72; Листов: 108
Пров.							
ГИП							
Н. контр.						**Кухня (пом. 1). Столешница: план** М 1:20	**Кырлан Александр Сергеевич**
Утв.							

Шкафы. Монтажная схема


крепление к стене, установочные размеры, зазоры под отделку · размеры в мм

ПРЕДВАРИТЕЛЬНО · не для производства работ · открыто пунктов: 9 (реестр — л. 6, 7)

Шкаф-купе М9 (пом. 5) (М 1:25)

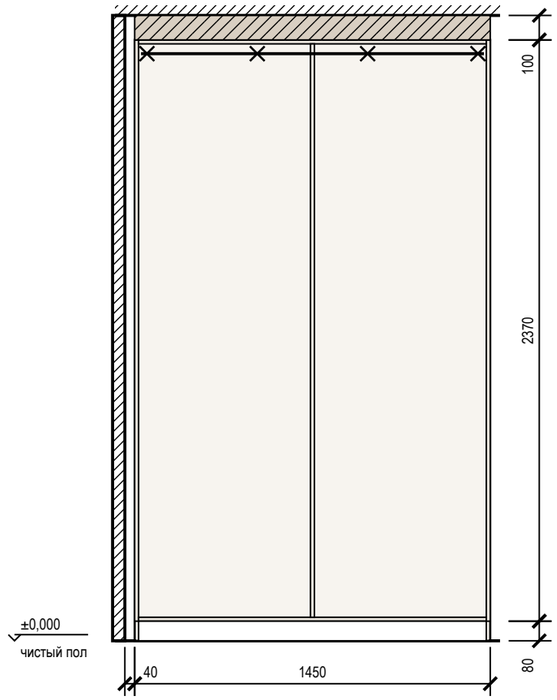

Система хранения Г1 (пом. 6) (М 1:25)

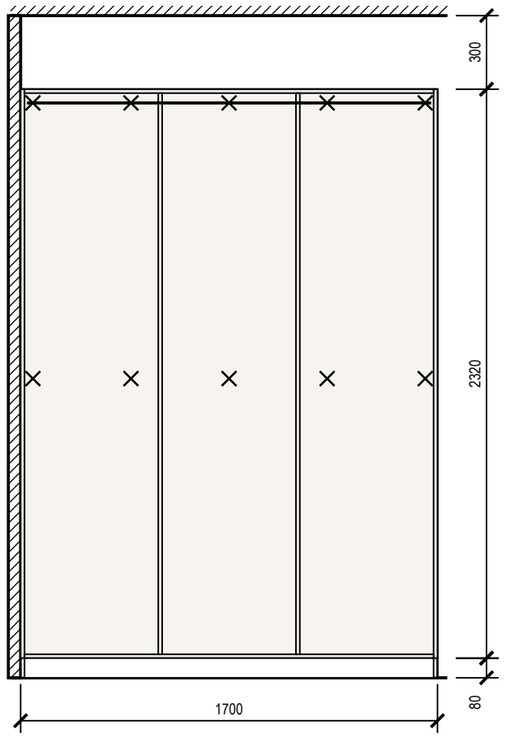

Крепление и зазоры под отделку

Марка	Помещение, стена	Основание	Отделка стены	Зазор, мм	Крепёж по планке	От опрокидывания
М9	Прихожая (5), стена В	по основанию — см. таблицу крепежа	окраска	5	анкер 4 шт., шаг 450	уголки 2 шт.
Г1	Гардеробная (6), стена Б	по основанию — см. таблицу крепежа	окраска	5	анкер 10 шт. (2 ряда)	крепление к стене, 3 точки

Крепёж по основанию стены

Основание стены	Крепёж
бетон, ж/б	анкер-шуруп 7,5×72 или дюбель 8×60 с шурупом 5×70
кирпич полнотелый	дюбель 8×80 с шурупом 5×90
газобетон, пазогребень	дюбель для газобетона 10×100 или химический анкер
гипсокартон	закладная до обшивки (брус 40×80 или фанера 18 мм), саморез в закладную

Условные обозначения

- анкер / уголок крепления к стене
- корпус и полки ЛДСП (вид на стену)
- компенсатор — короб до потолка

Примечания

1. Установочные размеры — от чистого пола и чистых стен; перед установкой контрольный замер после отделки.
2. Порядок: корпус выставить по уровню опорами цоколя → закрепить к стене по задней планке → навесить двери и фасады, отрегулировать зазоры → подогнать и закрепить компенсатор.
3. Анкеры — с шагом не более 500 мм, не ближе 50 мм от края планки; на ГКЛ только в закладную, установленную до обшивки.
4. Скрытые коммуникации под анкеры проверить детектором; трассы электрики по плану розеток.

Допущения и предложения на листе

Основа листа: размеры сняты с плана заказчика, контрольный обмер не выполнен (К-5); высота потолка 2700 мм принята: на плане заказчика не указана (К-5); подрайон климата не задан — принят не северный (жилые от 2,5 м) (К-4); толщины стен приняты: наружные 250 мм, перегородки 120 мм — не обмерены (К-5); разрешённая мощность 15 кВт принята по типовой квартире, технических условий нет (К-6).
См. лист открытых вопросов (лист 6, записи К-4–К-6).

1000 мм · печать 1:1

Изм.	Кол.уч	Лист	№ док.	Подп.	Дата
Разраб.		Кырлан А.С.			14.11.26
Пров.					
ГИП					
Н. контр.					
Утв.					

ГД-2026-006-АИ

Квартира 58 м²

Общая площадь 55,23* м² · * размеры приняты, не замерены (реестр — л. 6, 7, К-5)

Дизайн-проект интерьера

Стадия	Лист	Листов
РП	73	108

Шкафы. Монтажная схема

М 1:25

Кырлан Александр Сергеевич

выпуск 14.11.2026 № bcee049e32 · стр. 81 из 128

Ведомости изделий, техники и фурнитуры

встроенная мебель и кухонный гарнитур · размеры в мм

Ведомость изделий

Марка	Наименование	Пом.	Ш×Г×В, мм	Корпус	Фасад	Кромка, мм	Кол.
М9	Шкаф-купе	5	1450×600×2450	ЛДСП 16	ЛДСП 10 мм в алюминиевом профиле	0,4 / 1	1
Г1	Система хранения	6	1700×600×2400	ЛДСП 16	без фасадов	0,4 / 2 *	1
М11**	Ниша под стиральную машину 620: без корпуса, между боковинами соседних модулей, фасад на петлях к боковине соседнего модуля; цоколь съёмный	1	620×600×900	без корпуса	МДФ эмаль 18 мм — на дверь машины (навеска из её комплекта), цоколь		1
М7	Модуль нижний: ящики, варочная	1	600×600×900	ЛДСП 16	МДФ эмаль 18 мм	0,4 / 1	1
М10	Модуль навесной: полки	1	600×350×620	ЛДСП 16	МДФ эмаль 18 мм	0,4 / 1	1
М6	Модуль нижний: ящики	1	400×600×900	ЛДСП 16	МДФ эмаль 18 мм	0,4 / 1	1
М8	Модуль навесной: полки, сушка	1	1200×350×720	ЛДСП 16	МДФ эмаль 18 мм	0,4 / 1	1
М5	Модуль нижний: мойка	1	800×600×900	ЛДСП 16	МДФ эмаль 18 мм	0,4 / 1	1
М4	Место под холодильник отдельностоящий: без корпуса и фасада	1	600×650×2100 (место в ряду)	без корпуса	без фасада (прибор отдельностоящий)		

Ведомость встраиваемой техники

Поз.	Прибор	Ниша, вырез, мм	Вентиляция	Питание	Схема
М7	Варочная панель индукционная, 60 см	вырез в столешнице 560 × 490		М7, Н=150 — в соседнем модуле, за ящиком	по модели
М5	Мойка врезная / подстольная с сифоном	вырез по шаблону, ориентир 700 × 480		смеситель — выводы ВК	по модели
М4	Холодильник отдельностоящий	проём 600, зазор сверху ≥ 50	по паспорту модели	питание: точка ЭОМ не задана — вывод под прибор не делать до задания	по модели
М10	Вытяжка встраиваемая в навесной модуль, 60 см	низ ≥ 650 над панелью	воздуховод к вентканалу, короб до потолка	питание: точка ЭОМ не задана — вывод под прибор не делать до задания	по модели

Ведомость фурнитуры

№	Фурнитура	Тип, размер	Изделия	Кол.
1	Система дверей купе: профиль, направляющие, ролики	на 2 двери	М9	1
2	Ручка-профиль вертикальная	в цвет профиля	М9	2
3	Полкодержатель с фиксацией	ø5 мм	М9, Г1, М10, М8	56
4	Штанга овальная 30×15, L = 701	+ 2 держателя	М9	1
5	Полка для обуви выдвижная наклонная	ширина 701	М9	3
6	Опора регулируемая с цоколем на клипсах	ход 20 мм	М9, Г1	14
7	Анкер по основанию стены	по таблице крепежа	М9, Г1, М10, М8	20
8	Уголок крепления к стене от опрокидывания	стальной	М9, Г1	4
9	Штанга овальная 30×15, L = 545	+ 2 держателя	Г1	3
10	Петля накладная 110° с доводчиком	чашка 35 мм	М11**, М10, М8, М5	16
11	Ручка-профиль	латунь матовая	М11**, М7, М10, М6, М8, М5	14
12	Направляющие полного выдвижения с доводчиком NL 500	пара	М7, М6	6
13	Опора кухонная регулируемая 100–120 мм	+ клипса цоколя	М7, М6, М5	14
14	Навес регулируемый для навесного шкафа	пара на секцию	М10, М8	3
15	Шина монтажная	L = 540	М10	1
16	Сушка для посуды в шкаф	ширина 800	М8	1
17	Шина монтажная	L = 1140	М8	1

Допущения и предложения на листе

Основа листа: размеры сняты с плана заказчика, контрольный обмер не выполнен (К-5); высота потолка 2700 мм принята: на плане заказчика не указана (К-5); подрайон климата не задан — принят не северный (жилые от 2,5 м) (К-4); толщины стен приняты: наружные 250 мм, перегородки 120 мм — не обмерены (К-5); разрешённая мощность 15 кВт принята по типовой квартире, технических условий нет (К-6).

Знак «**» — предложение проектировщика, заказчиком не утверждено (согласовать с заказчиком): К-7: М11 — место стиральной машины: вместо модуля с ящиками 400 справа от варочной; ряд до 3420, журнальный стол М21 (с х 3440) не мешает загрузке.

См. лист открытых вопросов (лист 6, записи К-4–К-7).

Примечания

1. Модели техники выбирает заказчик до изготовления мебели; ниши, вырезы и вентиляция — по монтажной схеме выбранной модели (условие гарантии), её номер вносится в ведомость.
2. Количество фурнитуры — по чертежам изделий; запас крепежа 5 %. Аналоги — по характеристикам (доводчик, нагрузка, ход).
3. Цвет корпусов, фасадов и профилей — по колерной карте проекта. Кромка — скрытые / видимые торцы, мм.
4. * Кромка в данных изделия не задана: принята ПВХ 0,4 мм на скрытых торцах и 2 мм на видимых (по умолчанию для ЛДСП корпуса и МДФ фасада); заказчик или мебельщик подтверждает до раскроя.

Изм.	Кол.уч	Лист	№ док.	Подп.	Дата
Разраб.		Кырлан А.С.			14.11.26
Пров.					
ГИП					
Н. контр.					
Утв.					

ГД-2026-006-АИ

Квартира 58 м²

Общая площадь 55,23* м² · * размеры приняты, не замерены (реестр — л. 6, 7, К-5)

Дизайн-проект интерьера

Стадия	Лист	Листов
РП	74	108

Ведомости изделий, техники и фурнитуры

М б/м

Кырлан Александр Сергеевич

Сводка листовых материалов и кромки

ЛДСП, МДФ, ХДФ и кромка по изделиям · площади в м², кромка в пог. м

Листовые материалы по толщинам и декорам

Материал, декор	Назначение	Изделий	S, м²	S × 1,15*, м²
ЛДСП 16 мм*	корпус	2	17,59	20,23
ЛДСП 16 мм	корпус	5	6,86	7,89
ХДФ 4 мм	задняя стенка	7	9,99	11,49
ЛДСП 10 мм в алюминиевом профиле	фасад	1	3,33	3,83
МДФ эмаль 18 мм	фасад	6	3,04	3,49
Итого			**40,81**	**46,93**

Кромка по типам

Кромка	Толщина, мм	Длина, пог. м	+10 %*, пог. м
видимая (передний торец, торец фасада ЛДСП)	2	65,1	71,6
скрытая (задний торец деталей корпуса)	0,4	44,7	49,2

Изделия (8)

Изделие	Пом.	Корпус, м²	ХДФ, м²	Фасад, м²	Кромка, пог. м
М9 Шкаф-купе	5	7,73	3,44	3,33	40,3
Г1 Система хранения	6	9,86	3,94	0,00	34,4
М11** модуль кухни	1	0,00	0,00	0,47	0,0
М7 модуль кухни	1	1,35	0,46	0,45	5,9
М10 модуль кухни	1	0,97	0,37	0,37	5,9
М6 модуль кухни	1	1,18	0,30	0,30	4,9
М8 модуль кухни	1	1,85	0,86	0,85	11,4
М5 модуль кухни	1	1,52	0,61	0,60	6,9

Примечания

1. Площади — по моделям изделий листов мебельщика: боковины, дно, крыша (у нижнего кухонного модуля — дно и две царги по 100 мм), полки, стойки, задняя стенка ХДФ, цоколь, фасады. Коэффициент раскроя 1,15* — обрезь, пропилы и подбор рисунка; сводка — для заказа материала, раскрой делает цех.
2. Кромка: видимая — передний торец деталей корпуса и периметр фасада из ЛДСП; скрытая — задний торец деталей корпуса. Фасады из МДФ (эмаль, шпон) кромки не имеют. Толщина — из materials.edge изделий; где не задана — по умолчанию 2 и 0,4 мм*.
3. Не вошло: короба ящиков (в комплекте направляющих NL), столешница (лист «Столешница: план» и раскрой камня), остров, встроенная техника, покупные изделия.
4. * — значение принято по практике, не задано в данных.

Допущения и предложения на листе

Основа листа: размеры сняты с плана заказчика, контрольный обмер не выполнен (К-5); высота потолка 2700 мм принята: на плане заказчика не указана (К-5); подрайон климата не задан — принят не северный (жилые от 2,5 м) (К-4); толщины стен приняты: наружные 250 мм, перегородки 120 мм — не обмерены (К-5); разрешённая мощность 15 кВт принята по типовой квартире, технических условий нет (К-6).

Знак «**» — предложение проектировщика, заказчиком не утверждено (согласовать с заказчиком): пол пом. 1, 2, 6 — артикул изделия не выбран: позиция описана характеристиками («аналог по характеристикам»), артикул выбирается при закупке; К-7: М11 — место стиральной машины: вместо модуля с ящиками 400 справа от варочной; ряд до 3420, журнальный стол М21 (с х 3440) не мешает загрузке.

См. лист открытых вопросов (лист 6, записи К-4–К-7).

Изм.	Кол.уч	Лист	№ док.	Подп.	Дата
Разраб.		Кырлан А.С.			14.11.26
Пров.					
ГИП					
Н. контр.					
Утв.					

ГД-2026-006-АИ

Квартира 58 м²

Общая площадь 55,23* м² · * размеры приняты, не замерены (реестр — л. 6, 7, К-5)

Дизайн-проект интерьера

Стадия	Лист	Листов
РП	75	108

Сводка листовых материалов и кромки

М б/м

Кырлан Александр Сергеевич

09

Развёртки и узлы



Кырлан Александр Сергеевич

выпуск 14.11.2026 · bcee049e32 · стр. 84 из 128

Реестр марок отделки и позиций альбома

Реестр марок отделки (О ↔ позиции колерной карты) и марки позиций по видам

Реестр марок отделки альбома

Марка	Поверхность	Материал, изделие	Цвет, код	Помещения	Колер. карта
О1	стены	окраска, Tikkurila, шелковисто-матовая, подготовка Q3	NCS S 1002-Y50R	1	К1
О2	плинтус	плинтус МДФ, Orac Decor Luxxus, h 110 мм, SX184, шелковисто-матовая	NCS S 0300-N	1, 2, 5	К3
О3	потолок	окраска, Tikkurila, глубокоматовая	NCS S 0300-N	1, 2, 3, 4, 5	К2, К5
О4	пол	инженерная доска, аналог: инженерная доска, дуб натуральный, масло, 1-полосная, 14/4 мм		1, 2, 6	КМ1
О5	стены	окраска, Tikkurila, глубокоматовая, подготовка Q3	NCS S 1502-Y50R	2, 5	К4, К6
О6	стены	облицовка плиткой, Italon Charme Extra, 600×1200 мм, 610015000370	Italon 610015000370 «Charme Extra»	3, 4	КМ2
О7	пол	керамогранит, Kerama Marazzi Две Венеции / Риальто, 600×600 мм, SG651622R	Kerama Marazzi SG651622R «Две Венеции / Риальто»	3, 4, 5	КМ3
О8	стены	окраска, Tikkurila Harmony, матовая, подготовка Q3	Tikkurila V503 «Winter»	6	К7
О9	плинтус	плинтус МДФ, Orac Decor Luxxus, h 110 мм, SX184	Tikkurila V503 «Winter»	6	К9
О10	потолок	окраска, Tikkurila Anti-Reflex 2, глубокоматовая, подготовка Q3	Tikkurila V503 «Winter»	6	К8

Марки позиций альбома по видам

Префикс	Что обозначает, позиции	Листы
Д	двери: Д-1–Д-4	20–22
ОК	окна: ОК-1	20–22
Г, М, С	мебель и оборудование: Г1, М1**, М3–М10, М11**, М20, М21, М22**, С1–С3	23–27
П	сантехнические приборы: П1**, П3**, П4, П5, П6**, П20	38–46
ДК	декор (картины, зеркала, растения): ДК1**, ДК2**, ДК3**, ДК4**, ДК5**, ДК6**, ДК7**, ДК8**, ДК9**, ДК10**, ДК11**, ДК12**, ДК13**	1, 60–65
Т	текстиль (шторы, ковры): Т1**, Т2**, Т3**, Т4**, Т5**, Т6**, Т7**, Т8**, Т9**, Т10**, Т11**, Т12**, Т13**, Т14**	1, 60–65
Р	розетки: Р1–Р16, Р20**	28–35
ЭВ	выводы кабеля: ЭВ1–ЭВ3	28–35
S	выключатели: S1–S9	28–35
Св	светильники: Св1**, Св2**, Св3, Св4, Св5**, Св6–Св8, Св9**, Св10–Св12, Св16	28–35
ИП	извещатели: ИП1–ИП3	28–35
ТВ	розетки ТВ: ТВ1	28–35
LAN	розетки компьютерные: LAN1, LAN2	28–35
БП	блоки питания LED: БП1, БП2	28–35
КУП	электроустановочные изделия: КУП1	28–35
ЩК, ЩС**	щиты: ЩК, ЩС**	28–35
ДФ	домофон: ДФ1	28–35

Марки позиций альбома по видам (продолжение)

Префикс	Что обозначает, позиции	Листы
Ст В1, Ст К1, Ст Т3**	стояки (системы В1, Т3**, К1): Ст В1-1, Ст К1-1, Ст Т3-1	38–46
Ш	шахты и короба: Ш1	20–22
О	марки отделки (реестр альбома): О1–О10	2–5, 76–94
К, КМ	позиции колерной карты: К1–К9, КМ1–КМ3	57–59
Р	радиаторы отопления: Р-1–Р-3	36, 37

Примечания

1. Марка отделки О — одна на весь альбом: одна и та же отделка (материал, изделие, цвет, формат) на всех листах имеет одну марку; на развёртках и планах стоят марки этого реестра.
2. Столбец «Колер. карта» — позиции колерной карты (лист 57): К — окраска по коду цвета, КМ — материал без кода цвета; «Помещения» — номера по экспликации; количества — по ведомости отделки помещений (лист 56).
3. Марки позиций: один префикс — один вид позиций на весь альбом (двери Д, окна ОК, мебель М, сантехприборы П, декор ДК, текстиль Т, колерная карта К и КМ, радиаторы РО, розетки Р, выключатели S, светильники Св; стояки — «Ст» и система, например «Ст К1-1»). Совпадение префиксов у разных видов — замечание к исходным данным, при выпуске исправляется в модели.

Допущения и предложения на листе

Основа листа: размеры сняты с плана заказчика, контрольный обмер не выполнен (К-5); высота потолка 2700 мм принята: на плане заказчика не указана (К-5); подрайон климата не задан — принят не северный (жилые от 2,5 м) (К-4); толщины стен приняты: наружные 250 мм, перегородки 120 мм — не обмерены (К-5); разрешённая мощность 15 кВт принята по типовой квартире, технических условий нет (К-6).
Знак «**» — предложение проектировщика, заказчиком не утверждено (согласовать с заказчиком): Св2 — общий свет зоны гостиной над журнальным столом М21 (трек шёл вдоль края стола М3 по проходу); трековая система 4 × 950 лм: поток принят до нормы освещённости, модель и паспорт не выбраны; Св5 — трековая система 2 × 900 лм: светильник добавлен проектировщиком, поток принят до нормы освещённости, модель и паспорт не выбраны; Св1 — подвес висел над проходом без заданной высоты, а стол — без света над ним: подвес по оси стола М3; Св9 — свет у зеркала — над зеркалом у умывальника по его оси (свет на лицо, а не над сантехникой); ЩС — щит слаботочный: место и состав; пол пом. 1, 2, 6 — артикул изделия не выбран: позиция описана характеристиками («аналог по характеристикам»), артикул выбирается при закупке; ИЗ-2: М22 — Было х 4250 — место занял диван М1 (х 4450…5400 от у 1000); ИЗ-2, ИЗ-4: М1 — Было offset 1300…3500: торец дивана в 500 мм от стены В, правые 350 мм проёма Д-2 (3900…4800) упирались в диван; ИЗ-4: Т1, Т2, Т3, Т4, Т5, Т6, ДК1, ДК2, ДК3, ДК4, Т7, Т8, Т9, Т10, Т11, ДК5, ДК6, ДК7, ДК8, ДК9, ДК10, ДК11; ИЗ-5: Т12, Т13, Т14, ДК12, ДК13; К-2: П1 — ванна 1500 вместо 1600 — не заходит в проход перед проёмом Д-4; перед ванной 680 мм — глубина помещения; П3 — умывальник у стены В справа от ванны — перед ним свободно 750 мм, до стены Б 90 мм; К-7: М11 — место стиральной машины: вместо модуля с ящиками 400 справа от варочной; ряд до 3420, журнальный стол М21 (с х 3440) не мешает загрузке; П6 — стиральная машина на кухне: в ванной и санузле места нет; подвод ХВС с шаровым краном, слив — встраиваемый сифон с обратным клапаном (водяной затвор), отдельная группа 6 щита с УЗО 30 мА; Р20 — питание стиральной машины П6 — отдельная группа 6 (УЗО 30 мА); над столешницей в габарите машины, не за корпусом.
См. лист открытых вопросов (лист 6, записи К-2, К-4–К-7; лист 7, записи ИЗ-2, ИЗ-4, ИЗ-5).

Изм.	Кол.уч	Лист	№ док.	Подп.	Дата	ГД-2026-006-АИ			
						Квартира 58 м²			
						Общая площадь 55,23* м² · * размеры приняты, не замерены (реестр — л. 6, 7, К-5)			
Разраб.		Кырлан А.С.			14.11.26	Дизайн-проект интерьера	Стадия	Лист	Листов
Пров.							РП	76	108
ГИП									
						Реестр марок отделки и позиций альбома	Кырлан Александр Сергеевич		
Н. контр.						М б/м			
Утв.									

Схема расположения развёрток и узлов

План квартиры: марки развёрток по помещениям, выноски узлов, ведомость «марка → лист»



Развёртки и узлы: марка → лист

Марка	Помещение / узел	Лист
В	Кухня-гостиная (пом. 1)	78
А	Кухня-гостиная (пом. 1)	79
Б	Кухня-гостиная (пом. 1)	80
Г	Кухня-гостиная (пом. 1)	81
А	Спальня (пом. 2)	82
Б	Спальня (пом. 2)	83
В	Спальня (пом. 2)	84
А, Б	Ванная (пом. 3)	85
В, Г	Ванная (пом. 3)	86
А, Б	Санузел (пом. 4)	87
В, Г	Санузел (пом. 4)	88
А	Прихожая (пом. 5)	89
Б, Г	Прихожая (пом. 5)	90
В	Прихожая (пом. 5)	91
А	Гардеробная (пом. 6)	92
Б, Г	Гардеробная (пом. 6)	93
узел 1	Порог 15 мм: мокрая зона — смежное помещение	94
узел 2	Дверь скрытого монтажа в плоскости стены, плинтус	94
узел 3	Короб стояков К1-1 с люком и звукоизоляцией	94
узел 4	Гидроизоляция санузла: заход на стены 200 мм, примыкание ванны	94
узел 5	Плинтус МДФ 110×16 мм у окрашенной стены по доске (ламинату)	94
узел 6	Плинтус МДФ 110×16 мм у окрашенной стены по керамограниту (плитке)	94

Условные обозначения

- А — марка развёртки: буква стены, стрелка — взгляд
- выноска узла: над полкой — узел, под полкой — лист
- 1 — номер помещения, площадь м²

1000 мм · печать 1:1

Примечания

1. Развёртки — вид на стену изнутри помещения; буквы стен — одна система на весь альбом (как на листах выводов, плитки и отделки).
2. Стены без электроточек, мебели, декора и акцентной отделки развёрток не имеют: их отделка — по ведомости отделки помещений.
3. Узлы — на листе узлов; места применения — по выноскам этого листа и ведомости «марка → лист».

Допущения и предложения на листе

Основа листа: размеры сняты с плана заказчика, контрольный обмер не выполнен (К-5); высота потолка 2700 мм принята: на плане заказчика не указана (К-5); подрайон климата не задан — принят не северный (жилые от 2,5 м) (К-4); толщины стен приняты: наружные 250 мм, перегородки 120 мм — не обмерены (К-5); разрешённая мощность 15 кВт принята по типовой квартире, технических условий нет (К-6).
См. лист открытых вопросов (лист 6, записи К-4–К-6).

Изм.	Кол.уч	Лист	№ док.	Подп.	Дата
Разраб.		Кырлан А.С.			14.11.26
Пров.					
ГИП					
Н. контр.					
Утв.					

ГД-2026-006-АИ

Квартира 58 м²

Общая площадь 55,23* м² · * размеры приняты, не замерены (реестр — л. 6, 7, К-5)

Дизайн-проект интерьера

Стадия	Лист	Листов
РП	77	108

Схема расположения развёрток и узлов

М 1:50


Кырлан Александр Сергеевич

Развёртка стены В. Кухня-гостиная (пом. 1), кухонный фронт

Кухня-гостиная (пом. 1) · вид изнутри помещения · размеры в мм, отметки в м

ПРЕДВАРИТЕЛЬНО · не для производства работ · открыто пунктов: 9 (реестр — л. 6, 7)

Стена В (М 1:25)

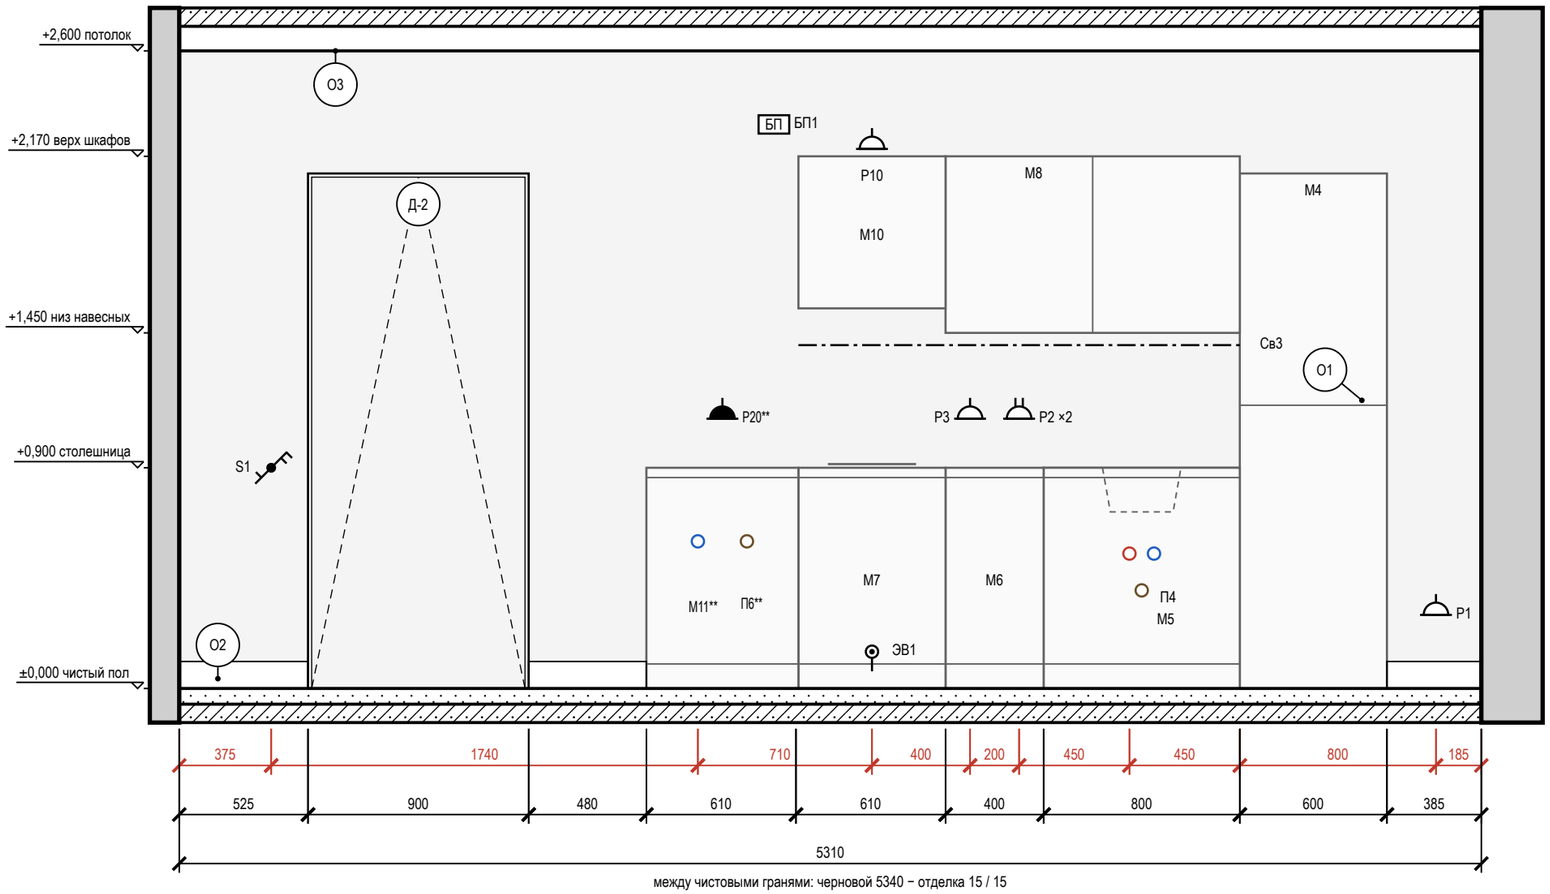

между чистовыми гранями: черновой 5340 − отделка 15 / 15

Условные обозначения

- розетка с заземляющим контактом; у знака — марка, ×N постов в рамке, гр. — группа щита, Н — высота оси, мм
- розетка влагозащищённая IP44
- вывод кабеля для подключения прибора (без розетки), марка ЭВ
- выключатель одноклавишный
- выключатель двухклавишный (флажков — по числу клавиш)
- выключатель с проходной или перекрёстной клавишей (обратный флажок); тип клавиши — в подписи
- светодиодная лента в профиле / в карнизе короба
- БП — блок питания LED, с доступом (люк от 100×100 мм)
- вывод В1 (код — в ведомости привязок)
- вывод Т3 (код — в ведомости привязок)
- вывод К1 (код — в ведомости привязок)
- привязки точек и выводов от угла и от пола, мм
- мебель и приборы — фасад по расстановке (условно)
- дверь скрытого монтажа: полотно в плоскости стены (узел — на листе узлов)
- стены и перекрытия в сечении
- О1 — марка отделки по реестру отделки альбома
- А — марка развёртки: буква стены, стрелка — взгляд

Допущения и предложения на листе. Основа листа: размеры сняты с плана заказчика, контрольный обмер не выполнен (К-5); высота потолка 2700 мм принята: на плане заказчика не указана (К-5); подрайон климата не задан — принят не северный (жилые от 2,5 м) (К-4); толщины стен приняты: наружные 250 мм, перегородки 120 мм — не обмерены (К-5); разрешённая мощность 15 кВт принята по типовой квартире, технических условий нет (К-6). Знак «**» — предложение проектировщика, заказчиком не утверждено (согласовать с заказчиком): К-7: М11 — место стиральной машины: вместо модуля с ящиками 400 справа от варочной; ряд до 3420, журнальный стол М21 (с х 3440) не мешает загрузке; П6 — стиральная машина на кухне: в ванной и санузле места нет; подвод ХВС с шаровым краном, слив — встраиваемый сифон с обратным клапаном (водяной затвор), отдельная группа 6 щита с УЗО 30 мА; Р20 — питание стиральной машины П6 — отдельная группа 6 (УЗО 30 мА); над столешницей в габарите машины, не за корпусом. См. лист открытых вопросов (лист 6, записи К-4–К-7).

Ведомость точек и выводов

Марка	Что это	Гр.	Н, мм	От угла, мм	Примечание
S1	выключатель	1	900	375	
В1-2	холодная вода — стиральная машина		600	2115	кран машины
Р20**	розетка: стиральная машина	6	1100	2215	IP44
К1-2	канализация — стиральная машина		600	2315	Ø40
БП1	блок питания LED	1	2300	2425	

Марка	Что это	Гр.	Н, мм	От угла, мм	Примечание
ЭВ1	вывод кабеля: варочная панель	3	150	2825	
Р10	розетка: вытяжка (встроена в дно М10)	2	2200	2825	
Р3	розетка: рабочая зона	2	1100	3225	
Р2	розетка: рабочая зона	2	1100	3425	рамка 2 поста
Т3-1	горячая вода — мойка кухонная		550	3875	межос. 100

Марка	Что это	Гр.	Н, мм	От угла, мм	Примечание
К1-1	канализация — мойка кухонная		400	3925	Ø50
В1-1	холодная вода — мойка кухонная		550	3975	межос. 100
Св3	светильник настенный	1	1400	4325	лента 2525–4325 от угла
Р1	розетка: холодильник	2	300	5125	

Примечания

1. Развёртки — вид на стену изнутри помещения, по часовой стрелке; расположение — на листе 77; размеры — в мм по чистовым поверхностям; отметки — в м от ±0,000; высоты Н — от чистого пола помещения до оси изделия, у декора — до центра.
2. Красная цепочка — привязки электроточек и выводов по осям от угла чистовых стен; высота Н — у знака, от чистого пола до оси; высоты мебели, проёмов и границ отделки — колонкой отметок слева. У знака — короткая марка; назначение, группа щита, высота и привязка каждой точки и вывода — в «Ведомости точек и выводов» под видами (каждая точка — строка).
3. Отделка стен — по ведомости отделки помещений, лист 56.
4. У знака электроточки: марка (Р — розетка, S — выключатель, Св — светильник, ЭВ — вывод кабеля), ×N — число постов в рамке, гр. — группа щита, Н — высота оси от чистого пола, мм; группы по клавишам выключателя — на листе выключателей.
5. Схема мебели, приборов и декора не является технической документацией для производства мебели; габариты — по паспортам изделий.
6. Двери скрытого монтажа — полотно в плоскости стены, отделка стены по полотну, плинтус прерывается у короба (узел — на листе узлов).
7. Выводы кухонной техники — по утверждённому проекту кухни: привязки выводов даются от осей модулей гарнитура.
8. Потолок — у каждой стены свой, по плану потолков (ПТ2); ступени — зоной, кромка короба перед нишей — тонкой линией; в поле потолка: ПТ1 +2,550.
9. Часть марок не уместилась у знаков: коды, высоты и привязки этих позиций — в ведомости точек и выводов под видами.

1000 мм · печать 1:1

Изм.	Кол.уч	Лист	№ док.	Подп.	Дата
Разраб.		Кырлан А.С.			14.11.26
Пров.					
ГИП					
Н. контр.					
Утв.					

ГД-2026-006-АИ

Квартира 58 м²

Общая площадь 55,23* м² · * размеры приняты, не замерены (реестр — л. 6, 7, К-5)

Дизайн-проект интерьера

Стадия	Лист	Листов
РП	78	108

Развёртка стены В. Кухня-гостиная (пом. 1), кухонный фронт

М 1:25

Кырлан Александр Сергеевич


выпуск 14.11.2026 № bcee049e32 · стр. 87 из 128

Развёртка стены А. Кухня-гостиная (пом. 1)

Кухня-гостиная (пом. 1) · вид изнутри помещения · размеры в мм, отметки в м

ПРЕДВАРИТЕЛЬНО · не для производства работ · открыто пунктов: 9 (реестр — л. 6, 7)

Стена А (М 1:25)

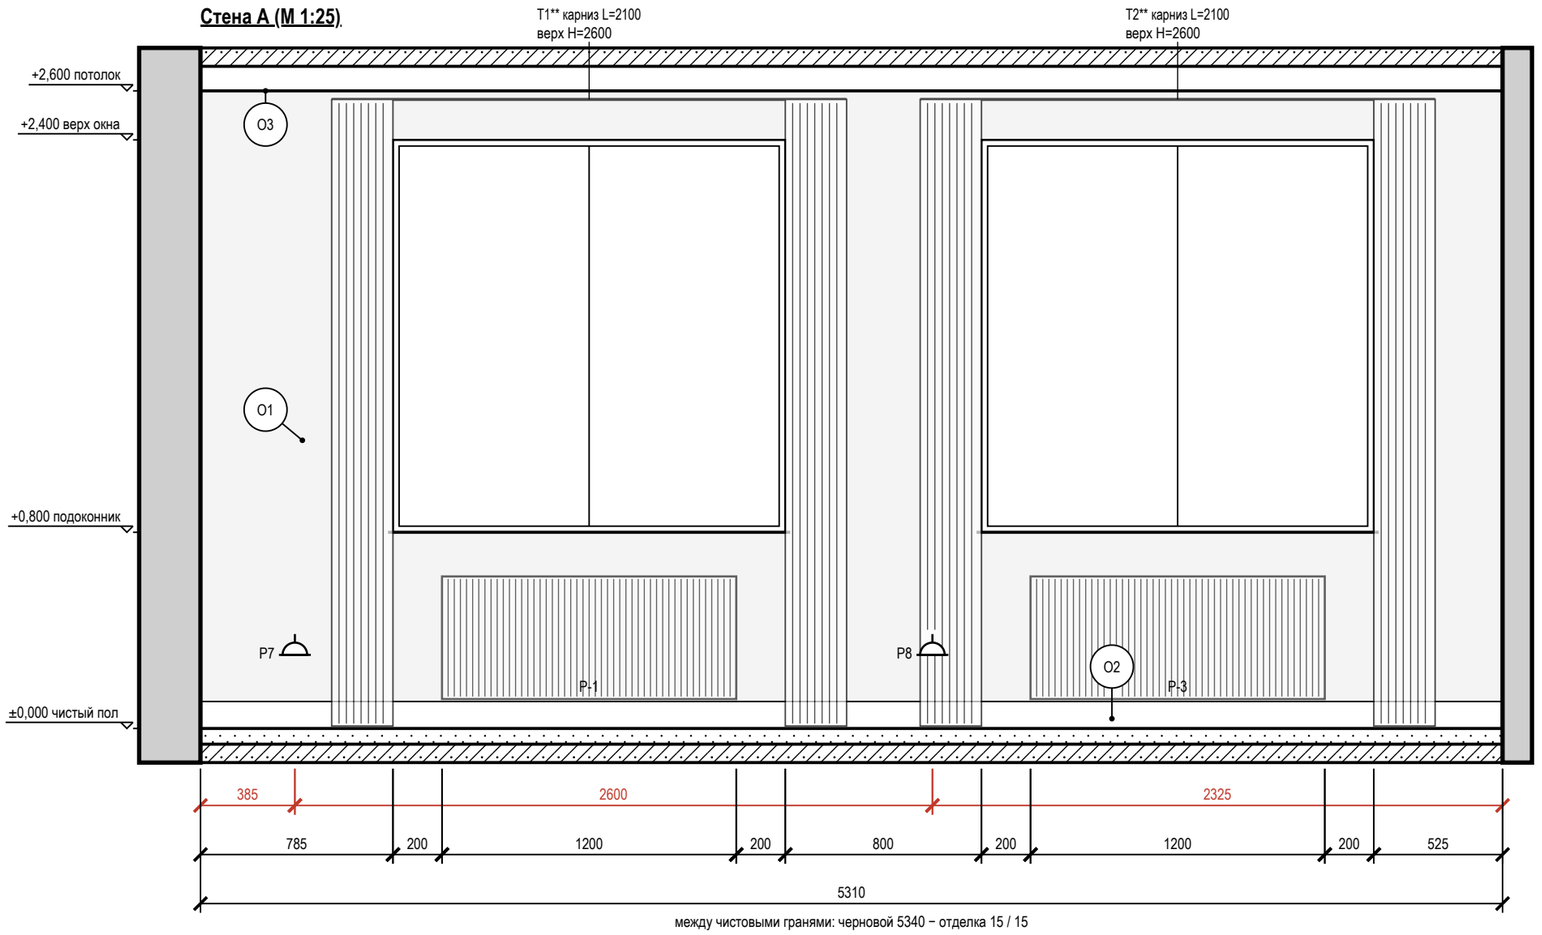


Условные обозначения

- розетка с заземляющим контактом; у знака — марка, ×N постов в рамке, гр. — группа щита, H — высота оси, мм
- привязки точек и выводов от угла и от пола, мм
- мебель и приборы — фасад по расстановке (условно)
- карниз (шина) и шторы в собранном виде: марка T, длина L, верх H
- окно: проём, рама, подоконник
- радиатор отопления; марка — по плану отопления
- стены и перекрытия в сечении
- O1 — марка отделки по реестру отделки альбома
- A — марка развёртки: буква стены, стрелка — взгляд

Ведомость отделки (на листе)

Марка	Поверхность	Материал, изделие	Цвет, код	Кол.
O1	стены	окраска, Tikkurila, шелковисто-матовая, подготовка Q3	NCS S 1002-Y50R	8,7 м²
O2	плинтус	плинтус МДФ, Orac Decor Luxxus, h 110 мм, SX184, шелковисто-матовая	NCS S 0300-N	5,3 м
O3	потолок	окраска, Tikkurila, глубокоматовая	NCS S 0300-N	21 м²

Схема развёрток (М 1:100)

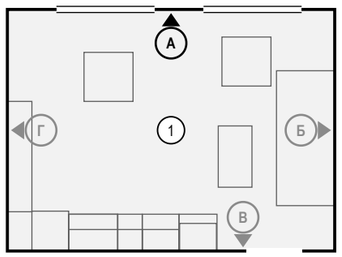

Ведомость точек и выводов

Марка	Что это	Гр.	H, мм	От угла, мм	Примечание
P7	розетка: торшер	4	300	385	
P8	розетка: зона отдыха	4	300	2985	

Ведомость изделий и проёмов (на листе)

Марка	Изделие, проём	На виде Ш×В, мм	Низ, мм
P-1	радиатор отопления	1200×500	120
P-3	радиатор отопления	1200×500	120

Примечания

1. Развёртки — вид на стену изнутри помещения, по часовой стрелке; расположение — на схеме листа и на листе 77; размеры — в мм по чистовым поверхностям; отметки — в м от ±0,000; высоты H — от чистого пола помещения до оси изделия, у декора — до центра.
2. Красная цепочка — привязки электроточек и выводов по осям от угла чистовых стен; высота H — у знака, от чистого пола до оси; высоты мебели, проёмов и границ отделки — колонкой отметок слева. У знака — короткая марка; назначение, группа щита, высота и привязка каждой точки и вывода — в «Ведомости точек и выводов» под видами (каждая точка — строка).
3. У знака электроточки: марка (P — розетка, S — выключатель, Св — светильник, ЭВ — вывод кабеля), ×N — число постов в рамке, гр. — группа щита, H — высота оси от чистого пола, мм; группы по клавишам выключателя — на листе выключателей.
4. Схема мебели, приборов и декора не является технической документацией для производства мебели; габариты — по паспортам изделий.
5. Карнизы (шины) — по ведомости текстиля декоратора: длина L и верх H на развёртке — те же числа, что в ведомости; крепление — до окраски потолка.
6. Потолок — у каждой стены свой, по плану потолков (ПТ2); ступени — зоной, кромка короба перед нишей — тонкой линией; в поле потолка: ПТ1 +2,550.
7. Линии узора (швы плитки, складки штор, рёбра радиаторов) прерываются у знаков и выносок — просвет между линиями не менее 0,7 мм.

Допущения и предложения на листе

Основа листа: размеры сняты с плана заказчика, контрольный обмер не выполнен (К-5); высота потолка 2700 мм принята: на плане заказчика не указана (К-5); подрайон климата не задан — принят не северный (жилые от 2,5 м) (К-4); толщины стен приняты: наружные 250 мм, перегородки 120 мм — не обмерены (К-5); разрешённая мощность 15 кВт принята по типовой квартире, технических условий нет (К-6).

Знак «**» — предложение проектировщика, заказчиком не утверждено (согласовать с заказчиком): ИЗ-4: Т1, Т2.

См. лист открытых вопросов (лист 6, записи К-4–К-6; лист 7, запись ИЗ-4).

1000 мм · печать 1:1

Изм.	Кол.уч	Лист	№ док.	Подп.	Дата
Разраб.		Кырлан А.С.			14.11.26
Пров.					
ГИП					
Н. контр.					
Утв.					

ГД-2026-006-АИ

Квартира 58 м²

Общая площадь 55,23* м² · * размеры приняты, не замерены (реестр — л. 6, 7, К-5)

Дизайн-проект интерьера

Стадия	Лист	Листов
РП	79	108

Развёртка стены А. Кухня-гостиная (пом. 1)

М 1:25

Кырлан Александр Сергеевич


выпуск 14.11.2026 № bcee049e32 · стр. 88 из 128

Развёртка стены Б. Кухня-гостиная (пом. 1)

Кухня-гостиная (пом. 1) · вид изнутри помещения · размеры в мм, отметки в м

ПРЕДВАРИТЕЛЬНО · не для производства работ · открыто пунктов: 9 (реестр — л. 6, 7)

Стена Б (М 1:20)

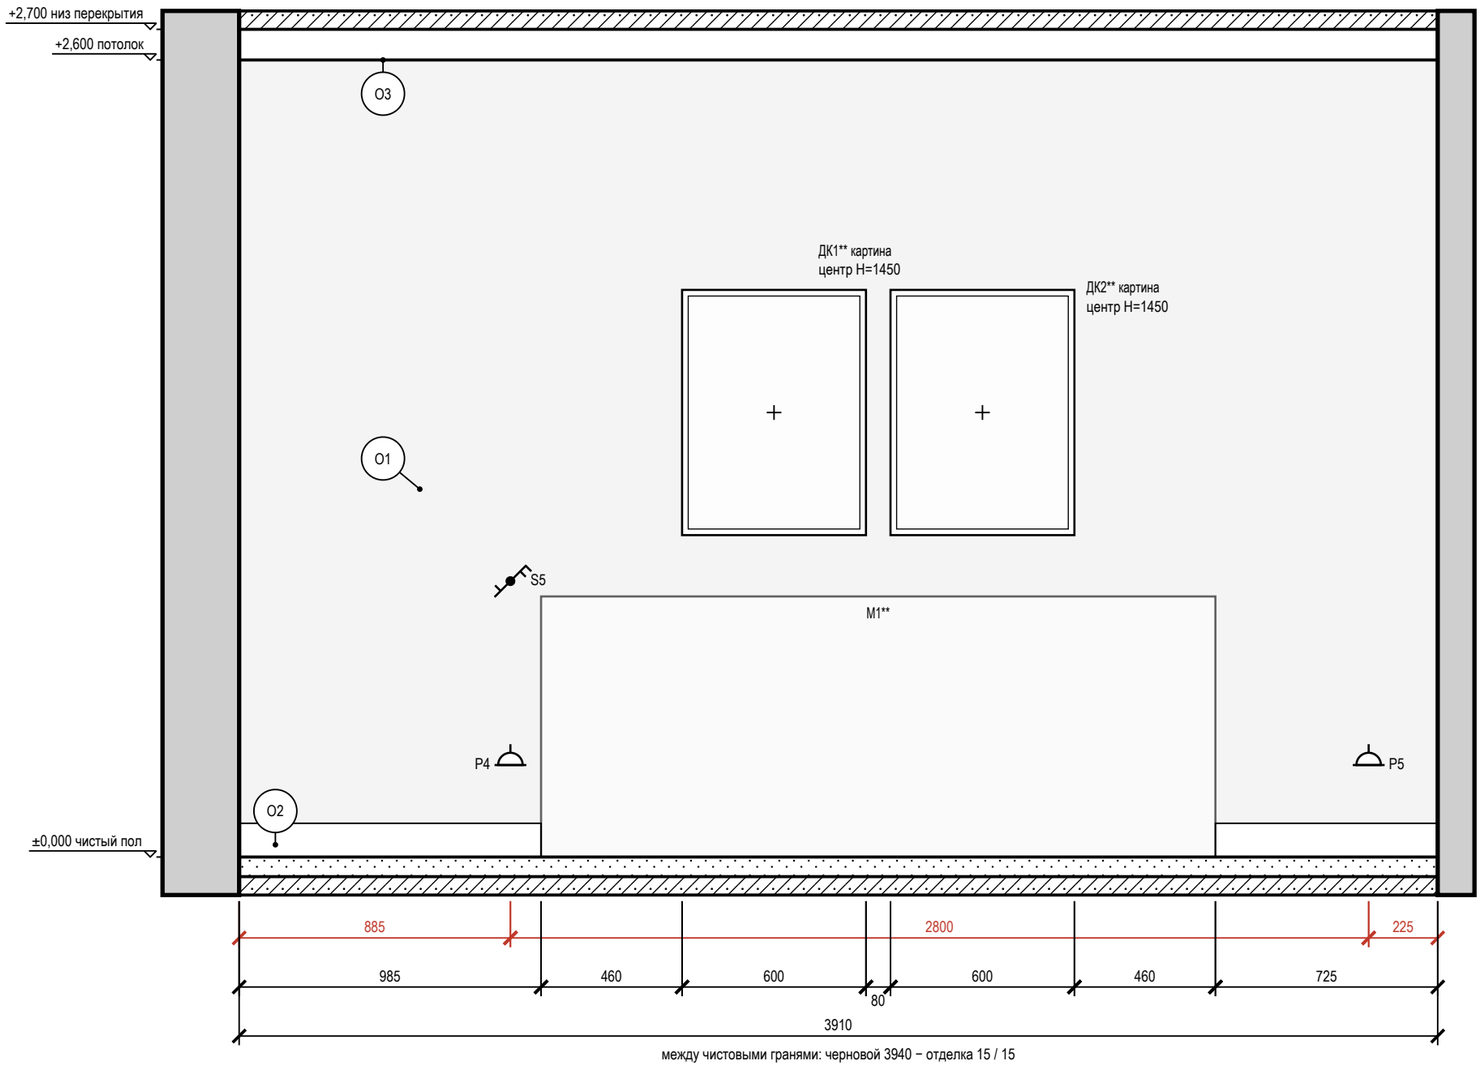

между чистовыми гранями: черновой 3940 − отделка 15 / 15

Ведомость точек и выводов

Марка	Что это	Гр.	Н, мм	От угла, мм	Примечание
Р4	розетка: у дивана	4	300	885	
S5	выключатель	1	900	885	
Р5	розетка: у дивана	4	300	3685	


Условные обозначения

- розетка с заземляющим контактом; у знака марка, ×N — постов в рамке, гр. — группа щита, Н — высота оси, мм
- выключатель одноклавишный
- выключатель двухклавишный (флажков — по числу клавиш)
- выключатель с проходной или перекрёстной клавишей (обратный флажок); тип клавиши — в подписи
- привязки точек и выводов от угла и от пола, мм
- мебель и приборы — фасад по расстановке (условно)
- картина (декор): марка Д, крест — центр, Н — высота центра, мм
- стены и перекрытия в сечении
- О1 — марка отделки по реестру отделки альбома
- А — марка развёртки: буква стены, стрелка взгляд

Ведомость отделки (на листе)

Марка	Поверхность	Материал, изделие	Цвет, код	Кол.
О1	стены	окраска, Tikkurila, шелковисто-матовая, подготовка Q3	NCS S 1002-Y50R	10,2 м²
О2	плинтус	плинтус МДФ, Orac Decor Luxxus, h 110 мм, SX184, шелковисто-матовая	NCS S 0300-N	1,7 м
О3	потолок	окраска, Tikkurila, глубокоматовая	NCS S 0300-N	21 м²

Схема развёрток (М 1:100)

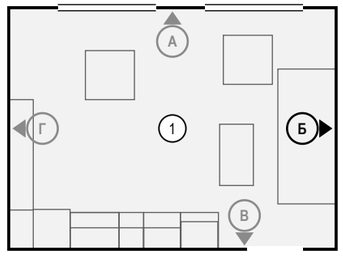

Примечания

1. Развёртки — вид на стену изнутри помещения, по часовой стрелке; расположение — на схеме листа и на листе 77; размеры — в мм по чистовым поверхностям; отметки — в м от ±0,000; высоты Н — от чистого пола помещения до оси изделия, у декора — до центра.
2. Красная цепочка — привязки электроточек и выводов по осям от угла чистовых стен; высота Н — у знака, от чистого пола до оси; высоты мебели, проёмов и границ отделки — колонкой отметок слева. У знака — короткая марка; назначение, группа щита, высота и привязка каждой точки и вывода — в «Ведомости точек и выводов» под видами (каждая точка — строка).
3. У знака электроточки: марка (Р — розетка, S — выключатель, Св — светильник, ЭВ — вывод кабеля), ×N — число постов в рамке, гр. — группа щита, Н — высота оси от чистого пола, мм; группы по клавишам выключателя — на листе выключателей.
4. Схема мебели, приборов и декора не является технической документацией для производства мебели; габариты — по паспортам изделий.
5. Картины и зеркала крепить к основанию по паспорту изделия (закладные и анкеры — в перечне скрытых работ); крест — ось центра предмета.
6. Потолок — у каждой стены свой, по плану потолков (ПТ2); ступени — зоной, кромка короба перед нишей — тонкой линией; в поле потолка: ПТ1 +2,550.

Допущения и предложения на листе

Основа листа: размеры сняты с плана заказчика, контрольный обмер не выполнен (К-5); высота потолка 2700 мм принята: на плане заказчика не указана (К-5); подрайон климата не задан — принят не северный (жилые от 2,5 м) (К-4); толщины стен приняты: наружные 250 мм, перегородки 120 мм — не обмерены (К-5); разрешённая мощность 15 кВт принята по типовой квартире, технических условий нет (К-6).

Знак «**» — предложение проектировщика, заказчиком не утверждено (согласовать с заказчиком): ИЗ-2, ИЗ-4: М1 — Было offset 1300…3500: торец дивана в 500 мм от стены В, правые 350 мм проёма Д-2 (3900…4800) упирались в диван; ИЗ-4: ДК1, ДК2.

См. лист открытых вопросов (лист 6, записи К-4–К-6; лист 7, записи ИЗ-2, ИЗ-4).

1000 мм · печать 1:1

Изм.	Кол.уч	Лист	№ док.	Подп.	Дата
Разраб.		Кырлан А.С.			14.11.26
Пров.					
ГИП					
Н. контр.					
Утв.					

ГД-2026-006-АИ

Квартира 58 м²

Общая площадь 55,23* м² · * размеры приняты, не замерены (реестр — л. 6, 7, К-5)

Дизайн-проект интерьера

Стадия	Лист	Листов
РП	80	108

Развёртка стены Б. Кухня-гостиная (пом. 1)

М 1:20

Кырлан Александр Сергеевич


выпуск 14.11.2026 № bcee049e32 · стр. 89 из 128

Развёртка стены Г. Кухня-гостиная (пом. 1)

Кухня-гостиная (пом. 1) · вид изнутри помещения · размеры в мм, отметки в м

ПРЕДВАРИТЕЛЬНО · не для производства работ · открыто пунктов: 9 (реестр — л. 6, 7)

Стена Г (М 1:20)

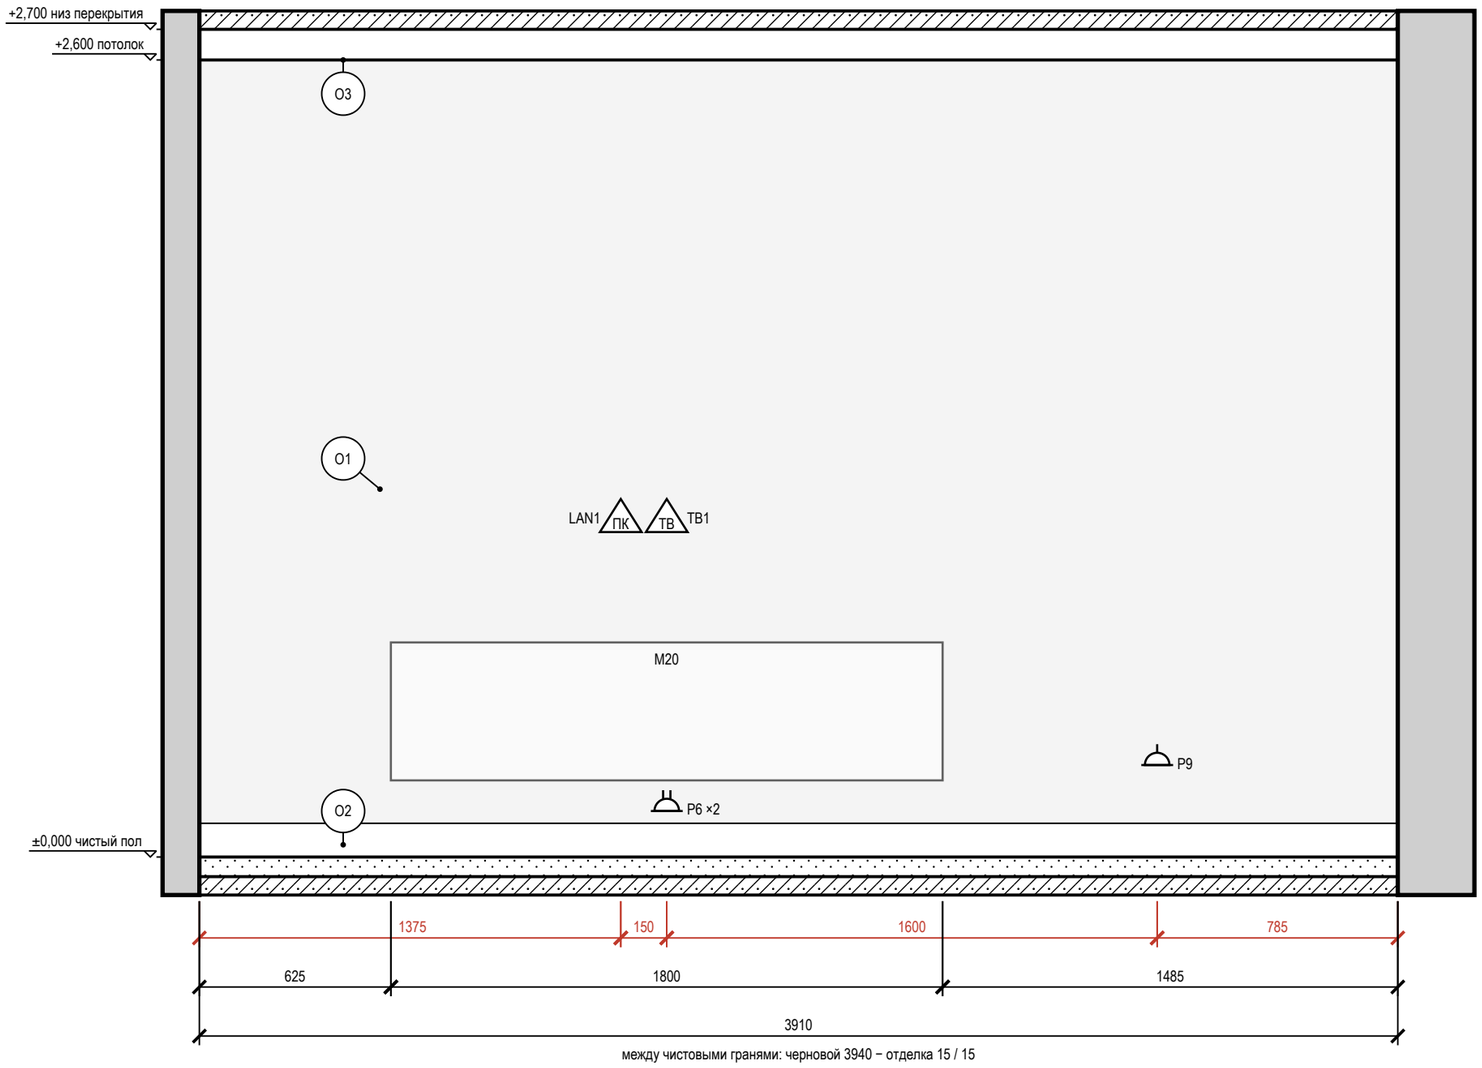

между чистовыми гранями: черновой 3940 − отделка 15 / 15

Ведомость точек и выводов

Марка	Что это	Гр.	Н, мм	От угла, мм	Примечание
LAN1	розетка RJ45: ТВ-приставка		1100	1375	
Р6	розетка: ТВ, приставка (за тумбой М20)	4	150	1525	рамка 2 поста
ТВ1	розетка ТВ: ТВ над тумбой М20		1100	1525	
Р9	розетка: обеденная зона	4	300	3125	


Условные обозначения

- розетка с заземляющим контактом; у знака марка, ×N — постов в рамке, гр. — группа щита, Н — высота оси, мм
- ПК — розетка компьютерная RJ45
- ТВ — розетка телевизионная
- привязки точек и выводов от угла и от пола, мм
- мебель и приборы — фасад по расстановке (условно)
- стены и перекрытия в сечении
- О1 — марка отделки по реестру отделки альбома
- А — марка развёртки: буква стены, стрелка взгляд

Ведомость отделки (на листе)

Марка	Поверхность	Материал, изделие	Цвет, код	Кол.
О1	стены	окраска, Tikkurila, шелковисто-матовая, подготовка Q3	NCS S 1002-Y50R	10,2 м²
О2	плинтус	плинтус МДФ, Orac Decor Luxxus, h 110 мм, SX184, шелковисто-матовая	NCS S 0300-N	3,9 м
О3	потолок	окраска, Tikkurila, глубокоматовая	NCS S 0300-N	21 м²

Схема развёрток (М 1:100)

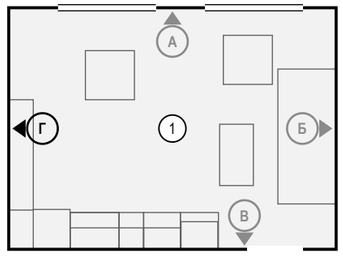

Примечания

1. Развёртки — вид на стену изнутри помещения, по часовой стрелке; расположение — на схеме листа и на листе 77; размеры — в мм по чистовым поверхностям; отметки — в м от ±0,000; высоты Н — от чистого пола помещения до оси изделия, у декора — до центра.
2. Красная цепочка — привязки электроточек и выводов по осям от угла чистовых стен; высота Н — у знака, от чистого пола до оси; высоты мебели, проёмов и границ отделки — колонкой отметок слева. У знака — короткая марка; назначение, группа щита, высота и привязка каждой точки и вывода — в «Ведомости точек и выводов» под видами (каждая точка — строка).
3. У знака электроточки: марка (Р — розетка, S — выключатель, Св — светильник, ЭВ — вывод кабеля), ×N — число постов в рамке, гр. — группа щита, Н — высота оси от чистого пола, мм; группы по клавишам выключателя — на листе выключателей.
4. Схема мебели, приборов и декора не является технической документацией для производства мебели; габариты — по паспортам изделий.
5. Потолок — у каждой стены свой, по плану потолков (ПТ2); ступени — зоной, кромка короба перед нишей — тонкой линией; в поле потолка: ПТ1 +2,550.

Допущения и предложения на листе

Основа листа: размеры сняты с плана заказчика, контрольный обмер не выполнен (К-5); высота потолка 2700 мм принята: на плане заказчика не указана (К-5); подрайон климата не задан — принят не северный (жилые от 2,5 м) (К-4); толщины стен приняты: наружные 250 мм, перегородки 120 мм — не обмерены (К-5); разрешённая мощность 15 кВт принята по типовой квартире, технических условий нет (К-6).

См. лист открытых вопросов (лист 6, записи К-4–К-6).

1000 мм · печать 1:1

Изм.	Кол.уч	Лист	№ док.	Подп.	Дата
Разраб.		Кырлан А.С.			14.11.26
Пров.					
ГИП					
Н. контр.					
Утв.					

ГД-2026-006-АИ

Квартира 58 м²

Общая площадь 55,23* м² · * размеры приняты, не замерены (реестр — л. 6, 7, К-5)

Дизайн-проект интерьера

Стадия	Лист	Листов
РП	81	108

Развёртка стены Г. Кухня-гостиная (пом. 1)

М 1:20


Кырлан Александр Сергеевич

выпуск 14.11.2026 № bcee049e32 · стр. 90 из 128

Развёртка стены А. Спальня (пом. 2)

Спальня (пом. 2) · вид изнутри помещения · размеры в мм, отметки в м

Стена А (М 1:20)

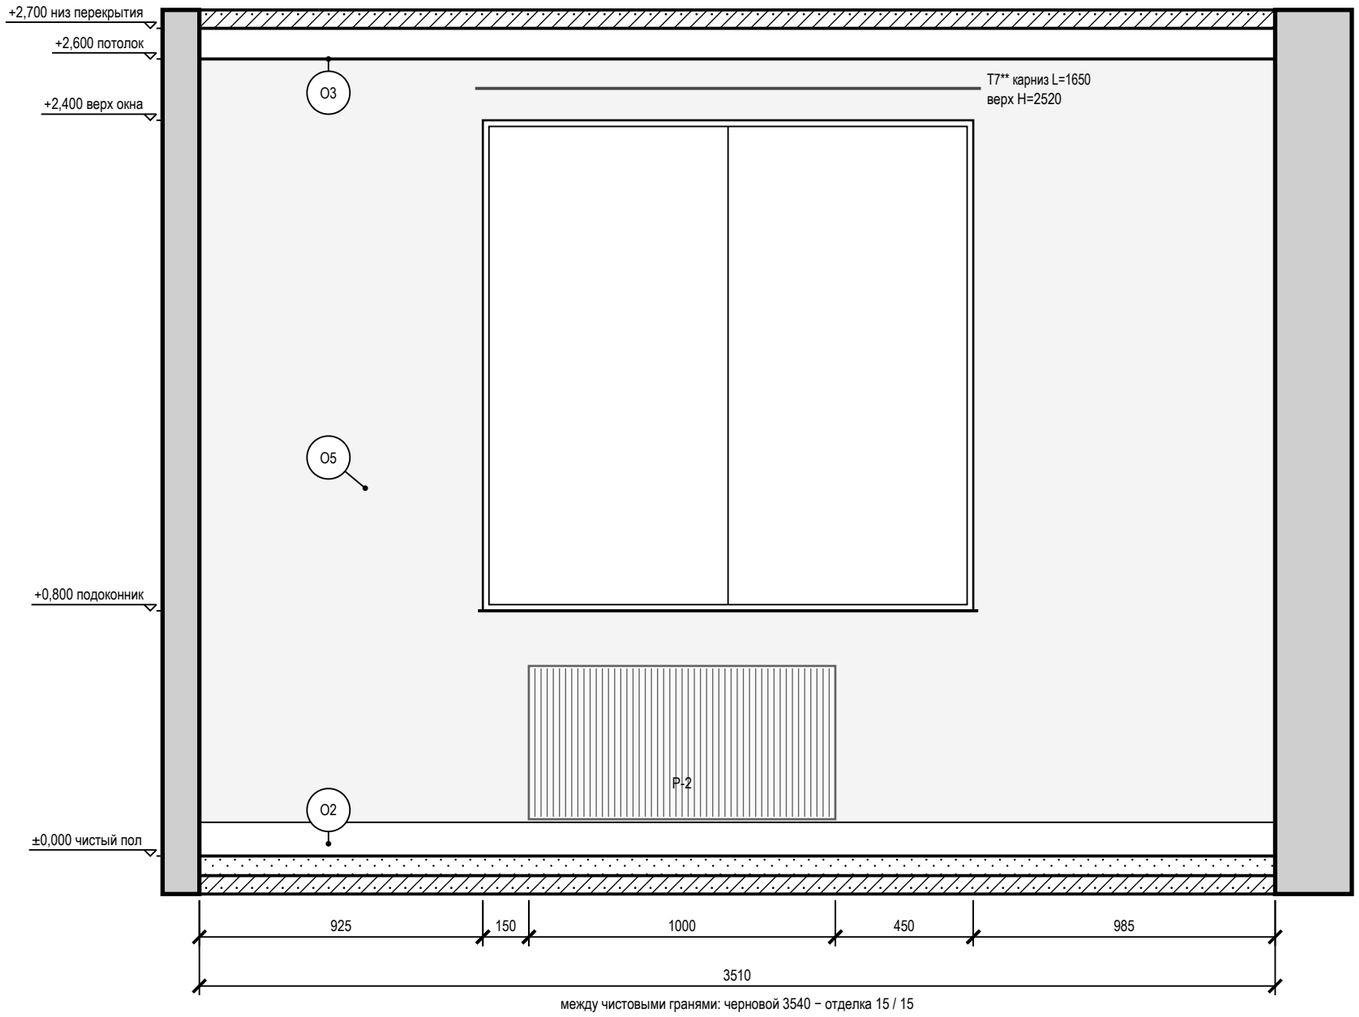

между чистовыми гранями: черновой 3540 − отделка 15 / 15


Условные обозначения

- мебель и приборы — фасад по расстановке (условно)
- карниз (шина) и шторы в собранном виде: марка Т, длина L, верх Н
- окно: проём, рама, подоконник
- радиатор отопления; марка — по плану отопления
- стены и перекрытия в сечении
- О1 — марка отделки по реестру отделки альбома
- А — марка развёртки: буква стены, стрелка взгляд

Ведомость отделки (на листе)

Марка	Поверхность	Материал, изделие	Цвет, код	Кол.
О2	плинтус	плинтус МДФ, Orac Decor Luxxus, h 110 мм, SX184, шелковисто-матовая	NCS S 0300-N	3,5 м
О3	потолок	окраска, Tikkurila, глубокоматовая	NCS S 0300-N	13,9 м²
О5	стены	окраска, Tikkurila, глубокоматовая, подготовка Q3	NCS S 1502-Y50R	6,6 м²

Схема развёрток (М 1:50)

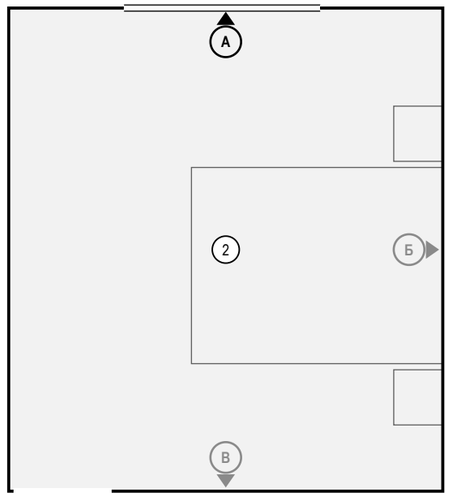

Ведомость изделий и проёмов (на листе)

Марка	Изделие, проём	На виде Ш×В, мм	Низ, мм
Р-2	радиатор отопления	1000×500	120

Примечания

1. Развёртки — вид на стену изнутри помещения, по часовой стрелке; расположение — на схеме листа и на листе 77; размеры — в мм по чистовым поверхностям; отметки — в м от ±0,000; высоты Н — от чистого пола помещения до оси изделия, у декора — до центра.
2. Схема мебели, приборов и декора не является технической документацией для производства мебели; габариты — по паспортам изделий.
3. Карнизы (шины) — по ведомости текстиля декоратора: длина L и верх Н на развёртке — те же числа, что в ведомости; крепление — до окраски потолка.
4. Потолок — у каждой стены свой, по плану потолков (ПТ2); ступени — зоной, кромка короба перед нишей — тонкой линией; в поле потолка: ПТ1 +2,550.

Допущения и предложения на листе

Основа листа: размеры сняты с плана заказчика, контрольный обмер не выполнен (К-5); высота потолка 2700 мм принята: на плане заказчика не указана (К-5); подрайон климата не задан — принят не северный (жилые от 2,5 м) (К-4); толщины стен приняты: наружные 250 мм, перегородки 120 мм — не обмерены (К-5); разрешённая мощность 15 кВт принята по типовой квартире, технических условий нет (К-6).

Знак «**» — предложение проектировщика, заказчиком не утверждено (согласовать с заказчиком): ИЗ-4: Т7.

См. лист открытых вопросов (лист 6, записи К-4–К-6; лист 7, запись ИЗ-4).

1000 мм · печать 1:1

Изм.	Кол.уч	Лист	№ док.	Подп.	Дата
Разраб.		Кырлан А.С.			14.11.26
Пров.					
ГИП					
Н. контр.					
Утв.					

ГД-2026-006-АИ

Квартира 58 м²

Общая площадь 55,23* м² · * размеры приняты, не замерены (реестр — л. 6, 7, К-5)

Дизайн-проект интерьера

Стадия	Лист	Листов
РП	82	108

Развёртка стены А. Спальня (пом. 2)

М 1:20


Кырлан Александр Сергеевич

Развёртка стены Б. Спальня (пом. 2)

Спальня (пом. 2) · вид изнутри помещения · размеры в мм, отметки в м

ПРЕДВАРИТЕЛЬНО · не для производства работ · открыто пунктов: 9 (реестр — л. 6, 7)

Стена Б (М 1:20)

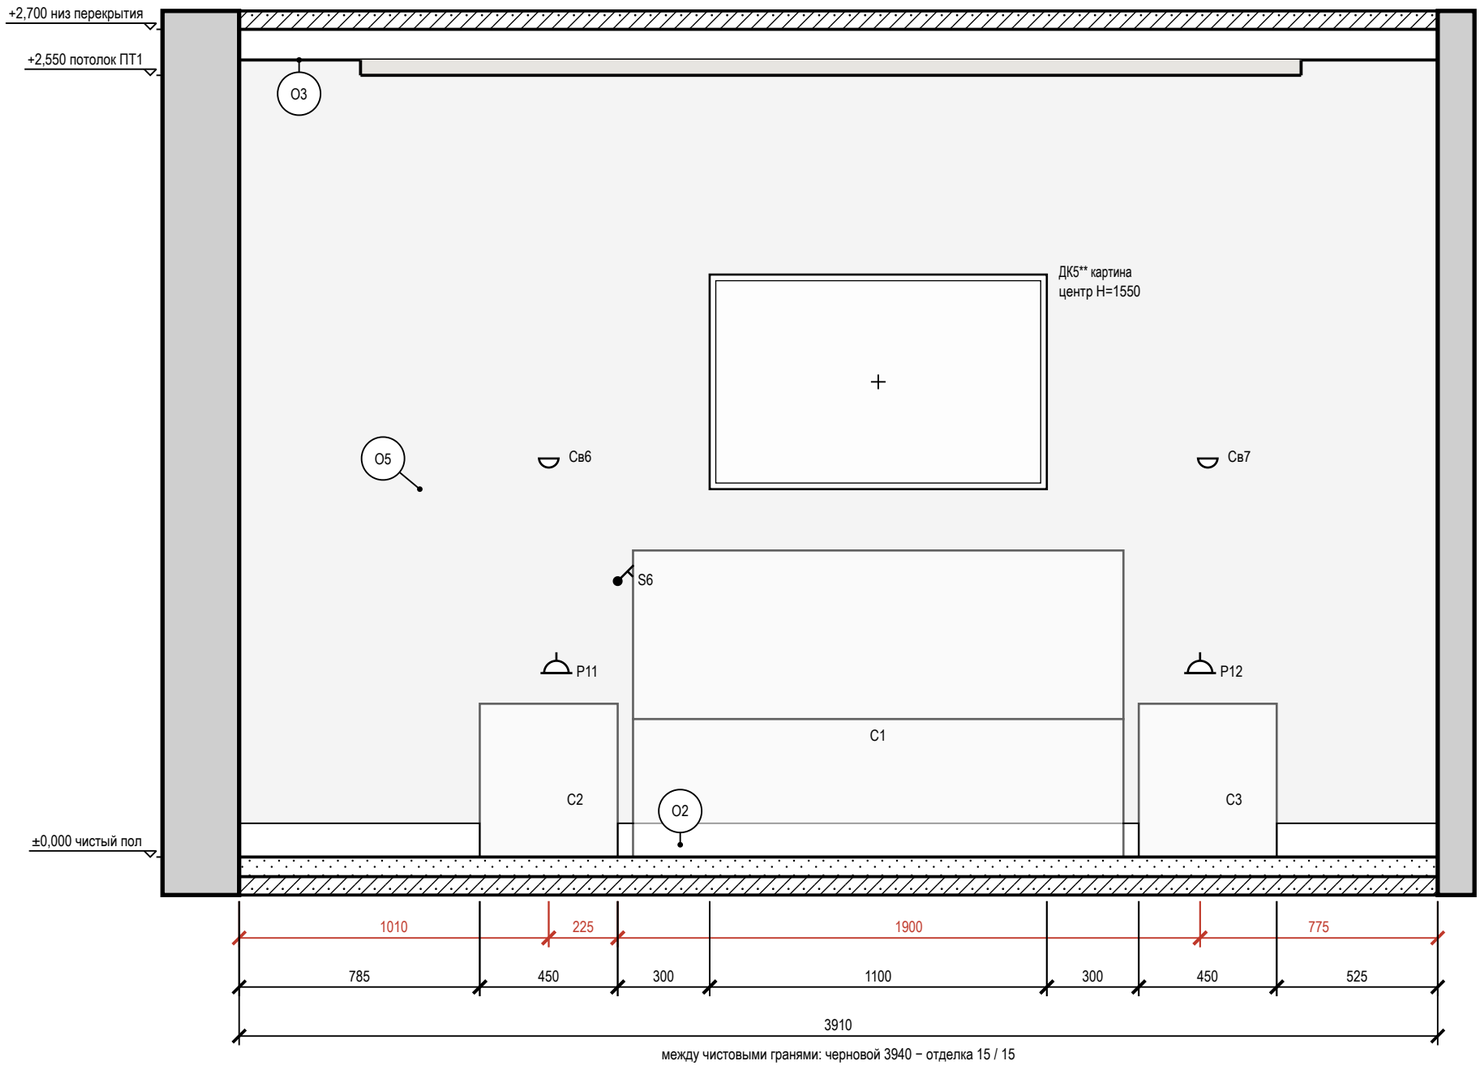

между чистовыми гранями: черновой 3940 − отделка 15 / 15

Ведомость точек и выводов

Марка	Что это	Гр.	Н, мм	От угла, мм	Примечание
Св6	светильник настенный	1	1300	1010	
Р11	розетка	4	600	1035	
S6	выключатель	1	900	1235	
Р12	розетка	4	600	3135	
Св7	светильник настенный	1	1300	3160	


Условные обозначения

- розетка с заземляющим контактом; у знака марка, ×N — постов в рамке, гр. — группа щита, Н — высота оси, мм
- выключатель одноклавишный
- светильник настенный (бра), Н — высота оси
- привязки точек и выводов от угла и от пола, мм
- мебель и приборы — фасад по расстановке (условно)
- картина (декор): марка Д, крест — центр, Н — высота центра, мм
- стены и перекрытия в сечении
- О1 — марка отделки по реестру отделки альбома
- А — марка развёртки: буква стены, стрелка взгляд

Ведомость отделки (на листе)

Марка	Поверхность	Материал, изделие	Цвет, код	Кол.
О2	плинтус	плинтус МДФ, Orac Decor Luxxus, h 110 мм, SX184, шелковисто-матовая	NCS S 0300-N	3 м
О3	потолок	окраска, Tikkurila, глубокоматовая	NCS S 0300-N	13,9 м²
О5	стены	окраска, Tikkurila, глубокоматовая, подготовка Q3	NCS S 1502-Y50R	10,2 м²

Схема развёрток (М 1:200)

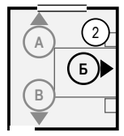

Примечания

1. Развёртки — вид на стену изнутри помещения, по часовой стрелке; расположение — на схеме листа и на листе 77; размеры — в мм по чистовым поверхностям; отметки — в м от ±0,000; высоты Н — от чистого пола помещения до оси изделия, у декора — до центра.
2. Красная цепочка — привязки электроточек и выводов по осям от угла чистовых стен; высота Н — у знака, от чистого пола до оси; высоты мебели, проёмов и границ отделки — колонкой отметок слева. У знака — короткая марка; назначение, группа щита, высота и привязка каждой точки и вывода — в «Ведомости точек и выводов» под видами (каждая точка — строка).
3. У знака электроточки: марка (Р — розетка, S — выключатель, Св — светильник, ЭВ — вывод кабеля), ×N — число постов в рамке, гр. — группа щита, Н — высота оси от чистого пола, мм; группы по клавишам выключателя — на листе выключателей.
4. Схема мебели, приборов и декора не является технической документацией для производства мебели; габариты — по паспортам изделий.
5. Картины и зеркала крепить к основанию по паспорту изделия (закладные и анкеры — в перечне скрытых работ); крест — ось центра предмета.
6. Потолок — у каждой стены свой, по плану потолков (ПТ2, ПТ1); ступени — зоной, кромка короба перед нишей — тонкой линией.

Допущения и предложения на листе

Основа листа: размеры сняты с плана заказчика, контрольный обмер не выполнен (К-5); высота потолка 2700 мм принята: на плане заказчика не указана (К-5); подрайон климата не задан — принят не северный (жилые от 2,5 м) (К-4); толщины стен приняты: наружные 250 мм, перегородки 120 мм — не обмерены (К-5); разрешённая мощность 15 кВт принята по типовой квартире, технических условий нет (К-6).

Знак «**» — предложение проектировщика, заказчиком не утверждено (согласовать с заказчиком): ИЗ-4: ДК5.

См. лист открытых вопросов (лист 6, записи К-4–К-6; лист 7, запись ИЗ-4).

1000 мм · печать 1:1

Изм.	Кол.уч	Лист	№ док.	Подп.	Дата
Разраб.		Кырлан А.С.			14.11.26
Пров.					
ГИП					
Н. контр.					
Утв.					

ГД-2026-006-АИ

Квартира 58 м²

Общая площадь 55,23* м² · * размеры приняты, не замерены (реестр — л. 6, 7, К-5)

Дизайн-проект интерьера

Стадия	Лист	Листов
РП	83	108

Развёртка стены Б. Спальня (пом. 2)

М 1:20

Кырлан Александр Сергеевич


выпуск 14.11.2026 № bcee049e32 · стр. 92 из 128

Развёртка стены В. Спальня (пом. 2)

Спальня (пом. 2) · вид изнутри помещения · размеры в мм, отметки в м

ПРЕДВАРИТЕЛЬНО · не для производства работ · открыто пунктов: 9 (реестр — л. 6, 7)

Стена В (М 1:20)

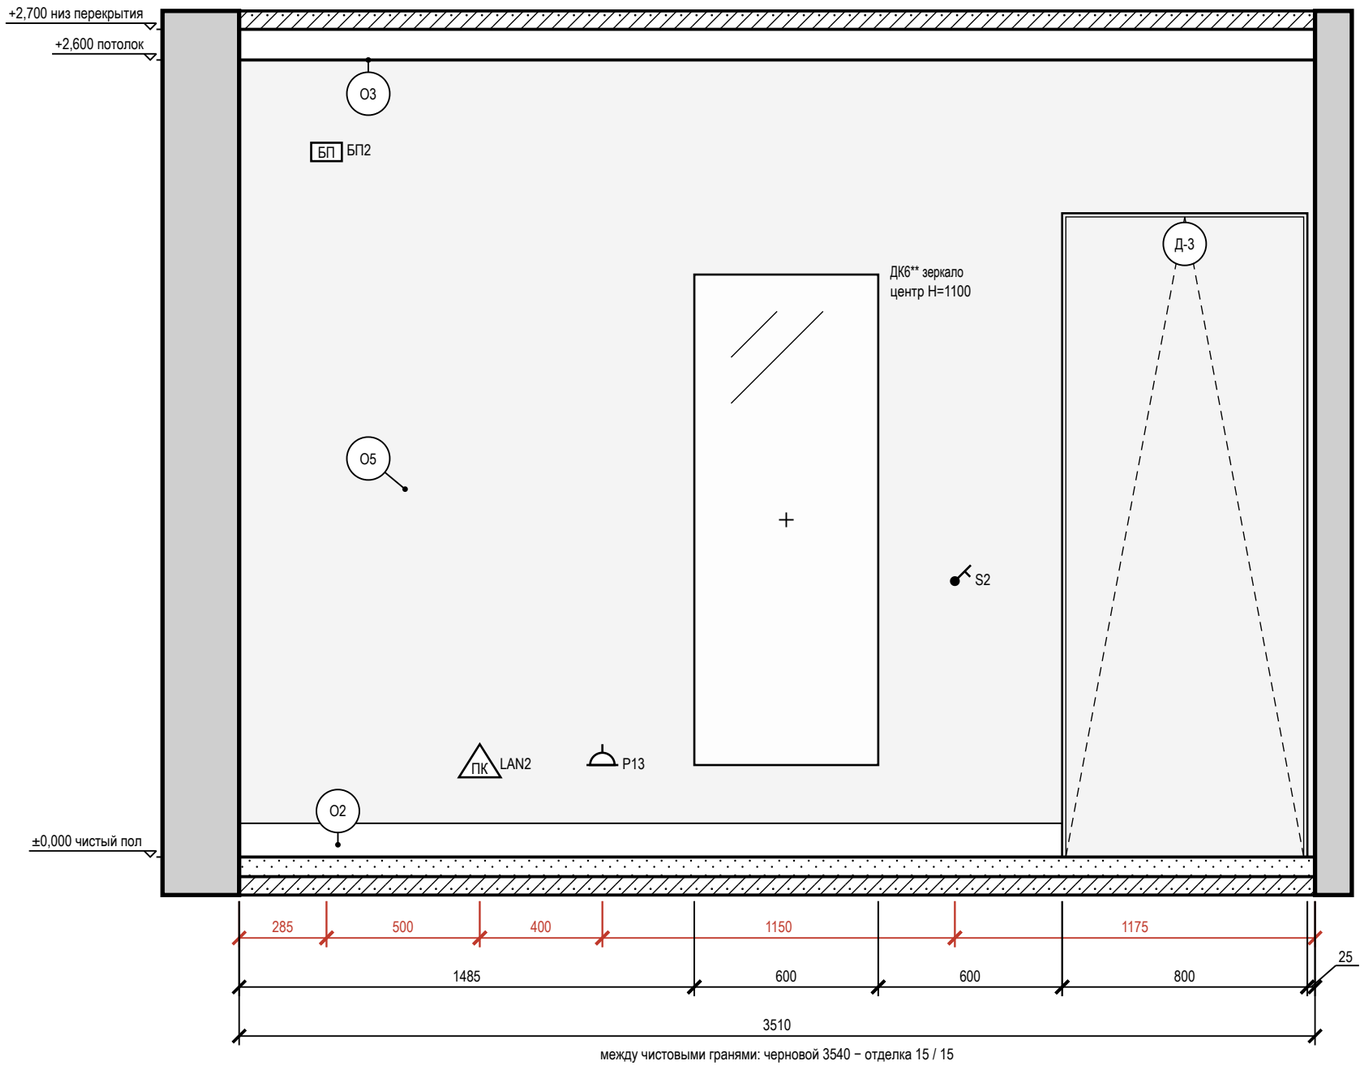

между чистовыми гранями: черновой 3540 − отделка 15 / 15

Ведомость точек и выводов

Марка	Что это	Гр.	H, мм	От угла, мм	Примечание
БП2	блок питания LED	1	2300	285	
LAN2	розетка RJ45: рабочее место, ТВ		300	785	
Р13	розетка: комод, зарядка	4	300	1185	
S2	выключатель	1	900	2335	


Условные обозначения

- розетка с заземляющим контактом; у знака марка, ×N — постов в рамке, гр. — группа щита, H — высота оси, мм
- выключатель одноклавишный
- БП — блок питания LED, с доступом (люк от 100×100 мм)
- ПК — розетка компьютерная RJ45
- привязки точек и выводов от угла и от пола, мм
- мебель и приборы — фасад по расстановке (условно)
- зеркало: марка Д, крест — центр, H — высота центра, мм
- дверь скрытого монтажа: полотно в плоскости стены (узел — на листе узлов)
- стены и перекрытия в сечении
- О1 — марка отделки по реестру отделки альбома
- A — марка развёртки: буква стены, стрелка взгляд

Ведомость отделки (на листе)

Марка	Поверхность	Материал, изделие	Цвет, код	Кол.
О2	плинтус	плинтус МДФ, Orac Decor Luxxus, h 110 мм, SX184, шелковисто-матовая	NCS S 0300-N	2,7 м
О3	потолок	окраска, Tikkurila, глубокоматовая	NCS S 0300-N	13,9 м²
О5	стены	окраска, Tikkurila, глубокоматовая, подготовка Q3	NCS S 1502-Y50R	7,4 м²

Схема развёрток (М 1:200)

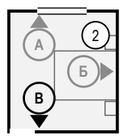

Примечания

1. Развёртки — вид на стену изнутри помещения, по часовой стрелке; расположение — на схеме листа и на листе 77; размеры — в мм по чистовым поверхностям; отметки — в м от ±0,000; высоты H — от чистого пола помещения до оси изделия, у декора — до центра.
2. Красная цепочка — привязки электроточек и выводов по осям от угла чистовых стен; высота H — у знака, от чистого пола до оси; высоты мебели, проёмов и границ отделки — колонкой отметок слева. У знака — короткая марка; назначение, группа щита, высота и привязка каждой точки и вывода — в «Ведомости точек и выводов» под видами (каждая точка — строка).
3. У знака электроточки: марка (Р — розетка, S — выключатель, Св — светильник, ЭВ — вывод кабеля), ×N — число постов в рамке, гр. — группа щита, H — высота оси от чистого пола, мм; группы по клавишам выключателя — на листе выключателей.
4. Схема мебели, приборов и декора не является технической документацией для производства мебели; габариты — по паспортам изделий.
5. Картины и зеркала крепить к основанию по паспорту изделия (закладные и анкеры — в перечне скрытых работ); крест — ось центра предмета.
6. Двери скрытого монтажа — полотно в плоскости стены, отделка стены по полотну, плинтус прерывается у короба (узел — на листе узлов).
7. Потолок — у каждой стены свой, по плану потолков (ПТ2); ступени — зоной, кромка короба перед нишей — тонкой линией; в поле потолка: ПТ1 +2,550.

Допущения и предложения на листе

Основа листа: размеры сняты с плана заказчика, контрольный обмер не выполнен (К-5); высота потолка 2700 мм принята: на плане заказчика не указана (К-5); подрайон климата не задан — принят не северный (жилые от 2,5 м) (К-4); толщины стен приняты: наружные 250 мм, перегородки 120 мм — не обмерены (К-5); разрешённая мощность 15 кВт принята по типовой квартире, технических условий нет (К-6).

Знак «**» — предложение проектировщика, заказчиком не утверждено (согласовать с заказчиком): ИЗ-4: ДК6.

См. лист открытых вопросов (лист 6, записи К-4–К-6; лист 7, запись ИЗ-4).

1000 мм · печать 1:1

Изм.	Кол.уч	Лист	№ док.	Подп.	Дата
Разраб.		Кырлан А.С.			14.11.26
Пров.					
ГИП					
Н. контр.					
Утв.					

ГД-2026-006-АИ

Квартира 58 м²

Общая площадь 55,23* м² · * размеры приняты, не замерены (реестр — л. 6, 7, К-5)

Дизайн-проект интерьера

Стадия	Лист	Листов
РП	84	108

Развёртка стены В. Спальня (пом. 2)

М 1:20

Кырлан Александр Сергеевич


выпуск 14.11.2026 № bcee049e32 · стр. 93 из 128

Развёртки стен А, Б. Ванная (пом. 3)

Ванная (пом. 3) · вид изнутри помещения · размеры в мм, отметки в м


ПРЕДВАРИТЕЛЬНО · не для производства работ · открыто пунктов: 9 (реестр — л. 6, 7)

Стена А (М 1:25)

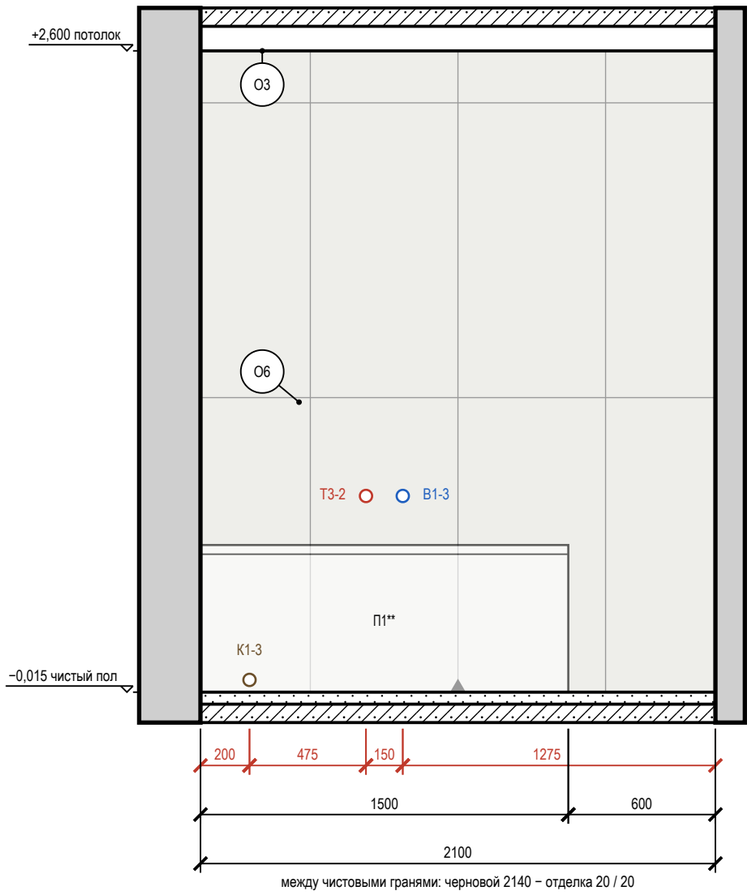

между чистовыми гранями: черновой 2140 − отделка 20 / 20

Стена Б (М 1:25)

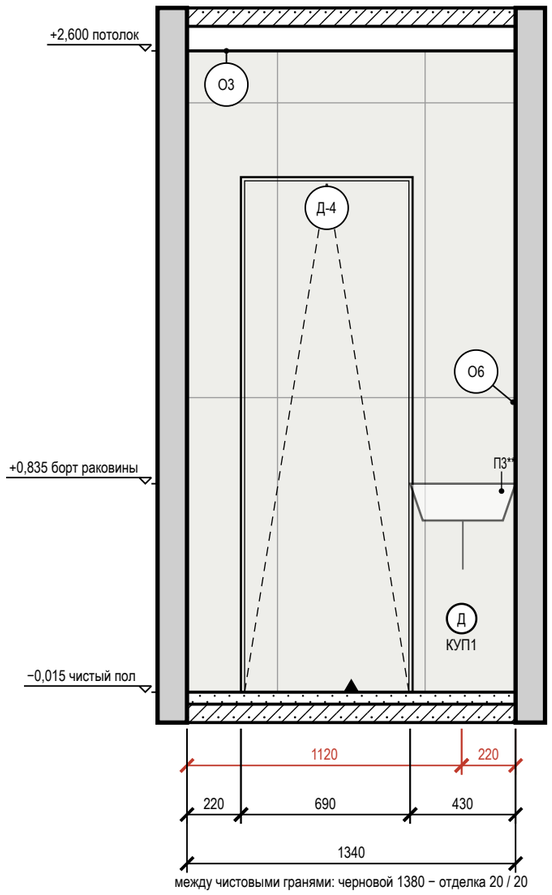

между чистовыми гранями: черновой 1380 − отделка 20 / 20

Условные обозначения

- вывод В1 (код — в ведомости привязок)
- вывод Т3 (код — в ведомости привязок)
- вывод К1 (код — в ведомости привязок)
- привязки точек и выводов от угла и от пола, мм
- мебель и приборы — фасад по расстановке (условно)
- дверь скрытого монтажа: полотно в плоскости стены (узел — на листе узлов)
- стены и перекрытия в сечении
- плитка: сетка швов по формату, ▲ — ось старта
- О1 — марка отделки по реестру отделки альбома
- А — марка развёртки: буква стены, стрелка взгляд

Ведомость отделки (на листе)

Марка	Поверхность	Материал, изделие	Цвет, код	Кол.
О3	потолок	окраска, Tikkurila, глубокоматовая	NCS S 0300-N	3 м²
О6	стены	облицовка плиткой, Italon Charme Extra, 600×1200 мм, 610015000370	Italon 610015000370 «Charme Extra»	7,5 м²

Схема развёрток (М 1:50)

Ведомость точек и выводов

Стена	Марка	Что это	Гр.	Н, мм	От угла, мм	Примечание
А	К1-3	канализация — ванна		50	200	Ø50
А	Т3-2	горячая вода — ванна		800	675	межос. 150

Стена	Марка	Что это	Гр.	Н, мм	От угла, мм	Примечание
А	В1-3	холодная вода — ванна		800	825	межос. 150
Б	КУП1	КУП (уравнивание потенциалов)		300	1120	

Ведомость изделий и проёмов (на листе)

Стена	Марка	Изделие, проём	На виде Ш×В, мм	Низ, мм
А	П1**	ванна	1500×600	0
Б	Д-4	дверь скрытого монтажа	700×2100	0
Б	П3**	умывальник	430×150	700

Примечания

1. Развёртки — вид на стену изнутри помещения, по часовой стрелке; расположение — на схеме листа и на листе 77; размеры — в мм по чистовым поверхностям; отметки — в м от ±0,000; высоты Н — от чистого пола помещения до оси изделия, у декора — до центра.
2. Красная цепочка — привязки электроточек и выводов по осям от угла чистовых стен; высота Н — у знака, от чистого пола до оси; высоты мебели, проёмов и границ отделки — колонкой отметок слева. У знака — короткая марка; назначение, группа щита, высота и привязка каждой точки и вывода — в «Ведомости точек и выводов» под видами (каждая точка — строка).
3. У знака электроточки: марка (Р — розетка, S — выключатель, Св — светильник, ЭВ — вывод кабеля), ×N — число постов в рамке, гр. — группа щита, Н — высота оси от чистого пола, мм; группы по клавишам выключателя — на листе выключателей.
4. Схема мебели, приборов и декора не является технической документацией для производства мебели; габариты — по паспортам изделий.
5. Облицовка — по сетке швов, раскладка от оси стены (треугольник у пола); подрезки — по листу раскладки плитки.
6. Гидроизоляция в 2 слоя, заход на стены 200 мм; над ванной — до 2000 и 300 мм за борт — до облицовки, с актом скрытых работ и тестом проливом (узел — на листе узлов).
7. Двери скрытого монтажа — полотно в плоскости стены, отделка стены по полотну, плинтус прерывается у короба (узел — на листе узлов).

Допущения и предложения на листе

Основа листа: размеры сняты с плана заказчика, контрольный обмер не выполнен (К-5); высота потолка 2700 мм принята: на плане заказчика не указана (К-5); подрайон климата не задан — принят не северный (жилые от 2,5 м) (К-4); толщины стен приняты: наружные 250 мм, перегородки 120 мм — не обмерены (К-5); разрешённая мощность 15 кВт принята по типовой квартире, технических условий нет (К-6).

Знак «**» — предложение проектировщика, заказчиком не утверждено (согласовать с заказчиком): К-2: П1 — ванна 1500 вместо 1600 — не заходит в проход перед проёмом Д-4; перед ванной 680 мм — глубина помещения; П3 — умывальник у стены В справа от ванны — перед ним свободно 750 мм, до стены Б 90 мм.

См. лист открытых вопросов (лист 6, записи К-2, К-4–К-6).

1000 мм · печать 1:1

Изм.	Кол.уч	Лист	№ док.	Подп.	Дата
Разраб.		Кырлан А.С.			14.11.26
Пров.					
ГИП					
Н. контр.					
Утв.					

ГД-2026-006-АИ

Квартира 58 м²

Общая площадь 55,23* м² · * размеры приняты, не замерены (реестр — л. 6, 7, К-5)

Дизайн-проект интерьера

Стадия	Лист	Листов
РП	85	108

Развёртки стен А, Б. Ванная (пом. 3)

М 1:25

Кырлан Александр Сергеевич


выпуск 14.11.2026 № bcee049e32 · стр. 94 из 128

Развёртки стен В, Г. Ванная (пом. 3)

Ванная (пом. 3) · вид изнутри помещения · размеры в мм, отметки в м


ПРЕДВАРИТЕЛЬНО · не для производства работ · открыто пунктов: 9 (реестр — л. 6, 7)

Стена В (М 1:25)

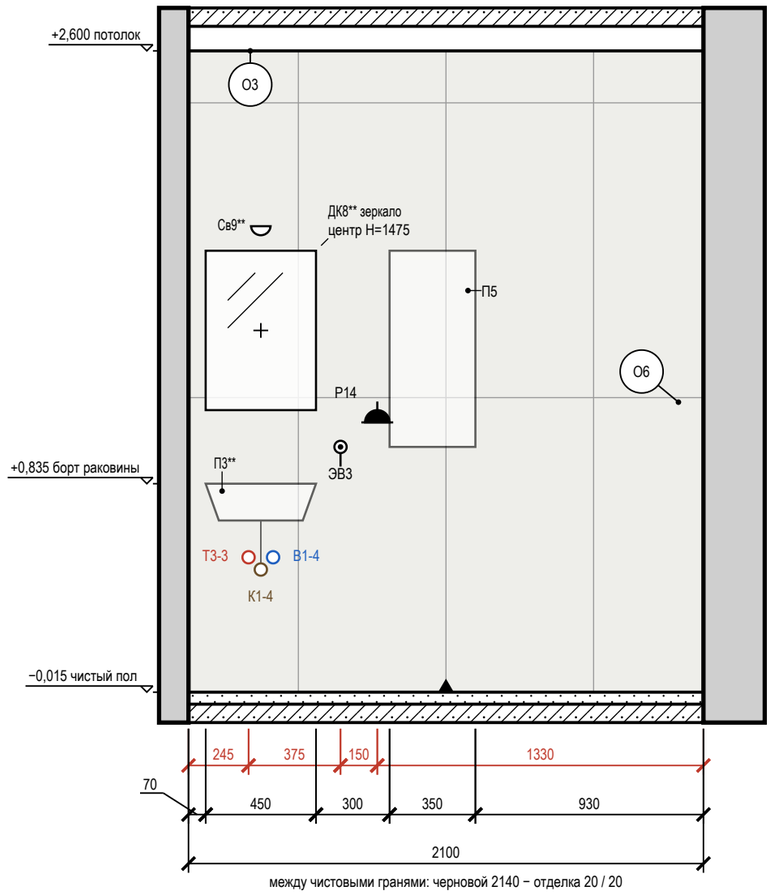

между чистовыми гранями: черновой 2140 − отделка 20 / 20

Стена Г (М 1:25)

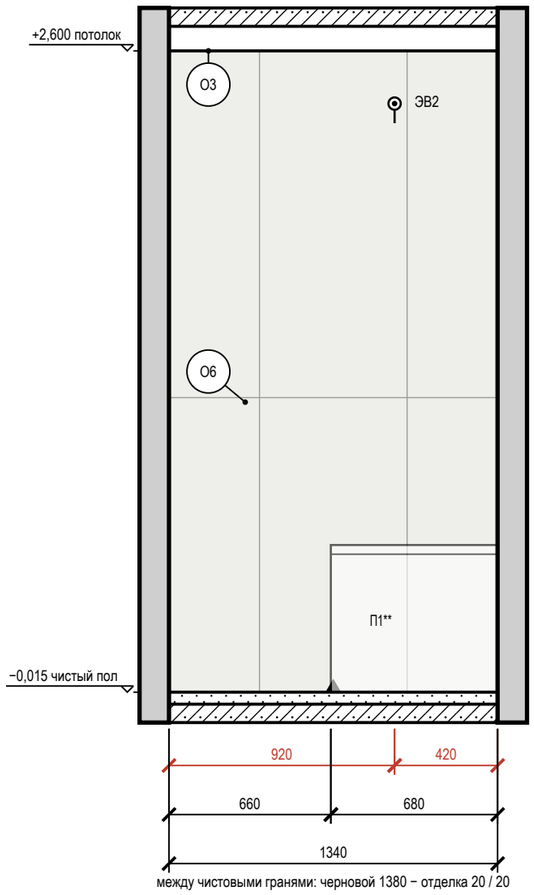

между чистовыми гранями: черновой 1380 − отделка 20 / 20

Ведомость точек и выводов

Стена	Марка	Что это	Гр.	Н, мм	От угла, мм	Примечание
В	Т3-3	горячая вода — умывальник		550	245	межос. 100
В	К1-4	канализация — умывальник		500	295	Ø50
В	Св9**	светильник настенный	1	1900	295	
В	В1-4	холодная вода — умывальник		550	345	межос. 100
В	ЭВ3	вывод кабеля: полотенцесушитель	5	1000	620	
В	Р14	розетка: фен	5	1100	770	IP44
Г	ЭВ2	вывод кабеля: вентилятор ВР2 (клавиша L4, таймер выбега)	1	2400	920	


Условные обозначения

- розетка влагозащищённая IP44
- вывод кабеля для подключения прибора (без розетки), марка ЭВ
- светильник настенный (бра), Н — высота оси
- вывод В1 (код — в ведомости привязок)
- вывод Т3 (код — в ведомости привязок)
- вывод К1 (код — в ведомости привязок)
- привязки точек и выводов от угла и от пола, мм
- мебель и приборы — фасад по расстановке (условно)
- зеркало: марка Д, крест — центр, Н — высота центра, мм
- стены и перекрытия в сечении
- плитка: сетка швов по формату, ▲ — ось старта
- О1 — марка отделки по реестру отделки альбома
- А — марка развёртки: буква стены, стрелка взгляд

Ведомость отделки (на листе)

Марка	Поверхность	Материал, изделие	Цвет, код	Кол.
О3	потолок	окраска, Tikkurila, глубокоматовая	NCS S 0300-N	3 м²
О6	стены	облицовка плиткой, Italon Charme Extra, 600×1200 мм, 610015000370	Italon 610015000370 «Charme Extra»	9 м²

Схема развёрток (М 1:50)

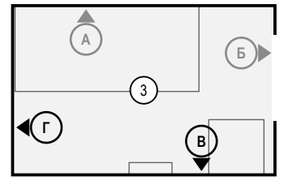

Примечания

1. Развёртки — вид на стену изнутри помещения, по часовой стрелке; расположение — на схеме листа и на листе 77; размеры — в мм по чистовым поверхностям; отметки — в м от ±0,000; высоты Н — от чистого пола помещения до оси изделия, у декора — до центра.
2. Красная цепочка — привязки электроточек и выводов по осям от угла чистовых стен; высота Н — у знака, от чистого пола до оси; высоты мебели, проёмов и границ отделки — колонкой отметок слева. У знака — короткая марка; назначение, группа щита, высота и привязка каждой точки и вывода — в «Ведомости точек и выводов» под видами (каждая точка — строка).
3. У знака электроточки: марка (Р — розетка, S — выключатель, Св — светильник, ЭВ — вывод кабеля), ×N — число постов в рамке, гр. — группа щита, Н — высота оси от чистого пола, мм; группы по клавишам выключателя — на листе выключателей.
4. Схема мебели, приборов и декора не является технической документацией для производства мебели; габариты — по паспортам изделий.
5. Облицовка — по сетке швов, раскладка от оси стены (треугольник у пола); подрезки — по листу раскладки плитки.
6. Гидроизоляция в 2 слоя, заход на стены 200 мм; над ванной — до 2000 и 300 мм за борт — до облицовки, с актом скрытых работ и тестом проливом (узел — на листе узлов).
7. Картины и зеркала крепить к основанию по паспорту изделия (закладные и анкеры — в перечне скрытых работ); крест — ось центра предмета.

Допущения и предложения на листе

Основа листа: размеры сняты с плана заказчика, контрольный обмер не выполнен (К-5); высота потолка 2700 мм принята: на плане заказчика не указана (К-5); подрайон климата не задан — принят не северный (жилые от 2,5 м) (К-4); толщины стен приняты: наружные 250 мм, перегородки 120 мм — не обмерены (К-5); разрешённая мощность 15 кВт принята по типовой квартире, технических условий нет (К-6).

Знак «**» — предложение проектировщика, заказчиком не утверждено (согласовать с заказчиком): Св9 — свет у зеркала — над зеркалом у умывальника по его оси (свет на лицо, а не над сантехникой); ИЗ-4: ДК8; К-2: П1 — ванна 1500 вместо 1600 — не заходит в проход перед проёмом Д-4; перед ванной 680 мм — глубина помещения; П3 — умывальник у стены В справа от ванны — перед ним свободно 750 мм, до стены Б 90 мм.

См. лист открытых вопросов (лист 6, записи К-2, К-4–К-6; лист 7, запись ИЗ-4).

1000 мм · печать 1:1

Изм.	Кол.уч	Лист	№ док.	Подп.	Дата
Разраб.		Кырлан А.С.			14.11.26
Пров.					
ГИП					
Н. контр.					
Утв.					

ГД-2026-006-АИ

Квартира 58 м²

Общая площадь 55,23* м² · * размеры приняты, не замерены (реестр — л. 6, 7, К-5)

Дизайн-проект интерьера

Стадия	Лист	Листов
РП	86	108

Развёртки стен В, Г. Ванная (пом. 3)

М 1:25

Кырлан Александр Сергеевич


выпуск 14.11.2026 № bcee049e32 · стр. 95 из 128

Развёртки стен А, Б. Санузел (пом. 4)

Санузел (пом. 4) · вид изнутри помещения · размеры в мм, отметки в м


ПРЕДВАРИТЕЛЬНО · не для производства работ · открыто пунктов: 9 (реестр — л. 6, 7)

Стена А (М 1:20)

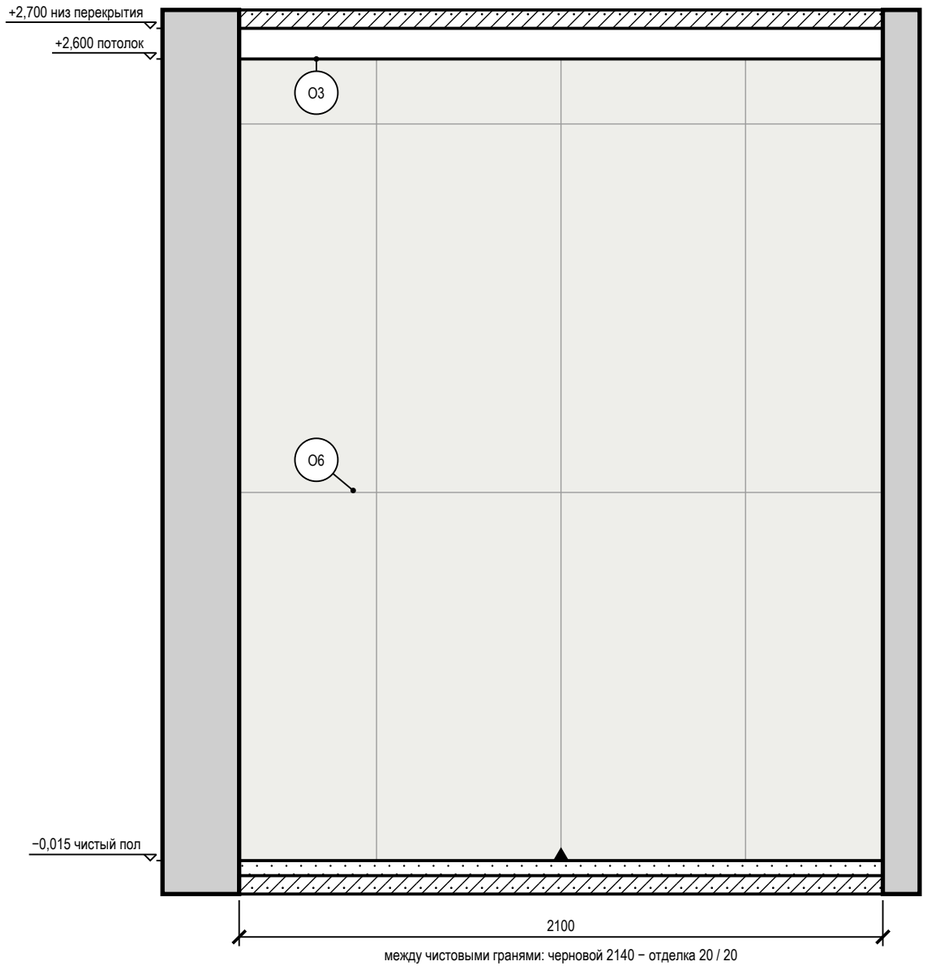

между чистовыми гранями: черновой 2140 − отделка 20 / 20

Стена Б (М 1:20)

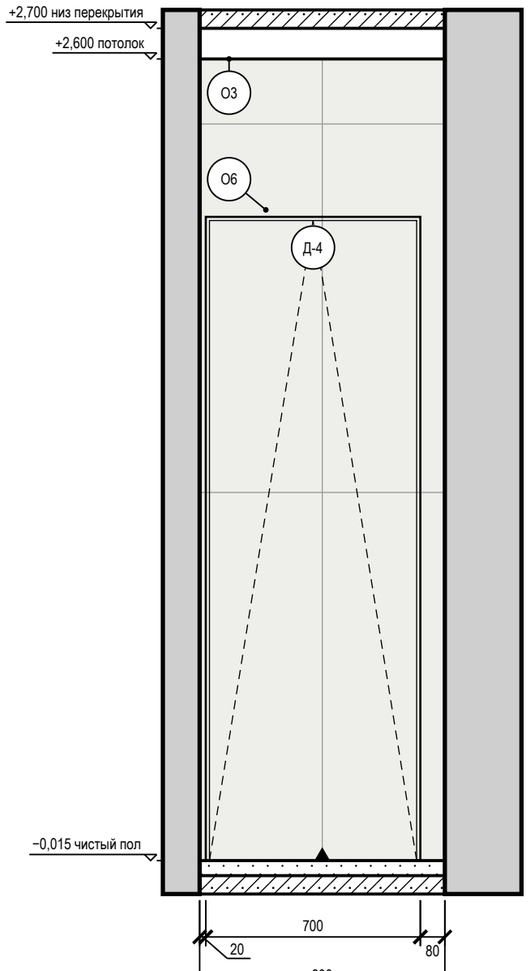

между чистовыми гранями: черновой 840 − отделка 20 / 20


Условные обозначения

- мебель и приборы — фасад по расстановке (условно)
- дверь скрытого монтажа: полотно в плоскости стены (узел — на листе узлов)
- стены и перекрытия в сечении
- плитка: сетка швов по формату, ▲ — ось старта
- О1 — марка отделки по реестру отделки альбома
- А — марка развёртки: буква стены, стрелка — взгляд

Ведомость отделки (на листе)

Марка	Поверхность	Материал, изделие	Цвет, код	Кол.
О3	потолок	окраска, Tikkurila, глубокоматовая	NCS S 0300-N	1,8 м²
О6	стены	облицовка плиткой, Italon Charme Extra, 600×1200 мм, 610015000370	Italon 610015000370 «Charme Extra»	6,1 м²

Схема развёрток (М 1:50)

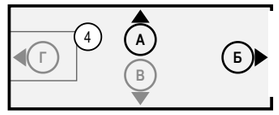

Ведомость изделий и проёмов (на листе)

Стена	Марка	Изделие, проём	На виде Ш×В, мм	Низ, мм
Б	Д-4	дверь скрытого монтажа	700×2100	0

Примечания

1. Развёртки — вид на стену изнутри помещения, по часовой стрелке; расположение — на схеме листа и на листе 77; размеры — в мм по чистовым поверхностям; отметки — в м от ±0,000; высоты Н — от чистого пола помещения до оси изделия, у декора — до центра.
2. Схема мебели, приборов и декора не является технической документацией для производства мебели; габариты — по паспортам изделий.
3. Облицовка — по сетке швов, раскладка от оси стены (треугольник у пола); подрезки — по листу раскладки плитки.
4. Гидроизоляция в 2 слоя, заход на стены 200 мм — до облицовки, с актом скрытых работ и тестом проливом (узел — на листе узлов).
5. Двери скрытого монтажа — полотно в плоскости стены, отделка стены по полотну, плинтус прерывается у короба (узел — на листе узлов).

Допущения и предложения на листе

Основа листа: размеры сняты с плана заказчика, контрольный обмер не выполнен (К-5); высота потолка 2700 мм принята: на плане заказчика не указана (К-5); подрайон климата не задан — принят не северный (жилые от 2,5 м) (К-4); толщины стен приняты: наружные 250 мм, перегородки 120 мм — не обмерены (К-5); разрешённая мощность 15 кВт принята по типовой квартире, технических условий нет (К-6).

См. лист открытых вопросов (лист 6, записи К-4–К-6).

1000 мм · печать 1:1

Изм.	Кол.уч	Лист	№ док.	Подп.	Дата
Разраб.		Кырлан А.С.			14.11.26
Пров.					
ГИП					
Н. контр.					
Утв.					

ГД-2026-006-АИ

Квартира 58 м²

Общая площадь 55,23* м² · * размеры приняты, не замерены (реестр — л. 6, 7, К-5)

Дизайн-проект интерьера

Стадия	Лист	Листов
РП	87	108

Развёртки стен А, Б. Санузел (пом. 4)

М 1:20

Кырлан Александр Сергеевич


выпуск 14.11.2026 № bcee049e32 · стр. 96 из 128

Развёртки стен В, Г. Санузел (пом. 4)

Санузел (пом. 4) · вид изнутри помещения · размеры в мм, отметки в м


ПРЕДВАРИТЕЛЬНО · не для производства работ · открыто пунктов: 9 (реестр — л. 6, 7)

Стена В (М 1:20)

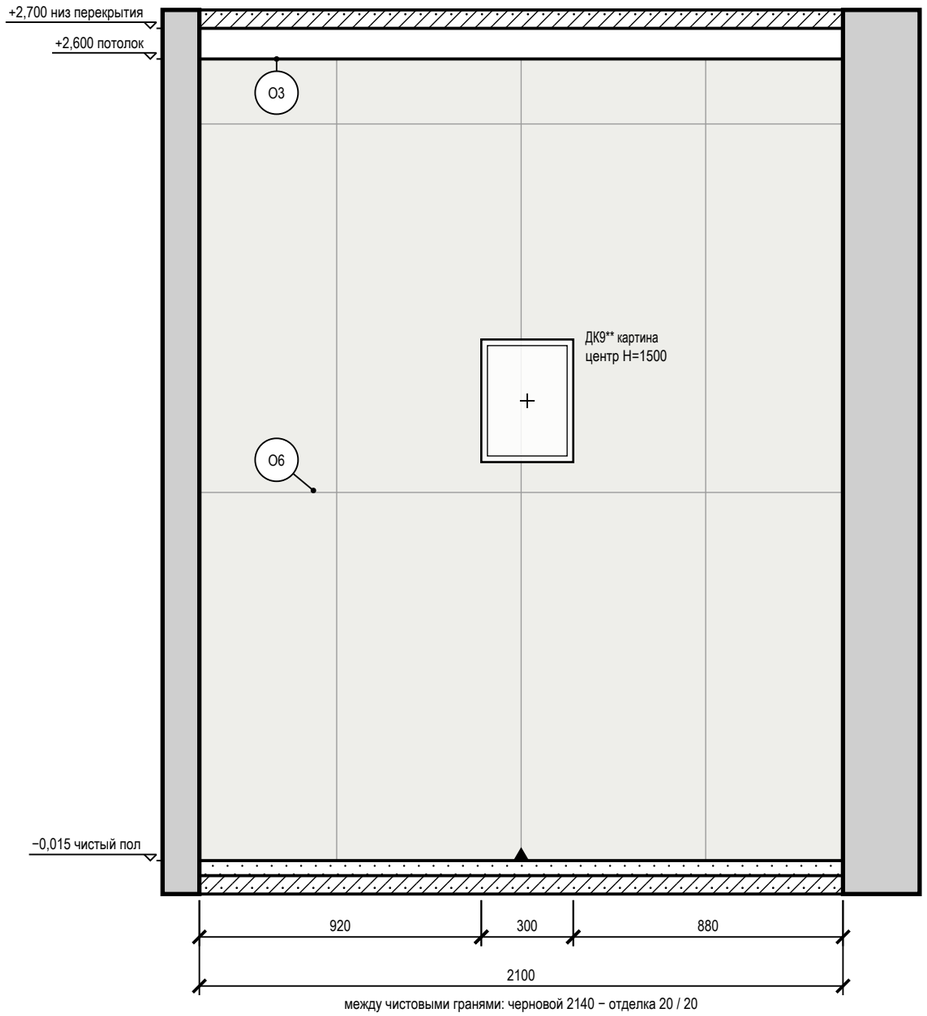

между чистовыми гранями: черновой 2140 − отделка 20 / 20

Стена Г (М 1:20)

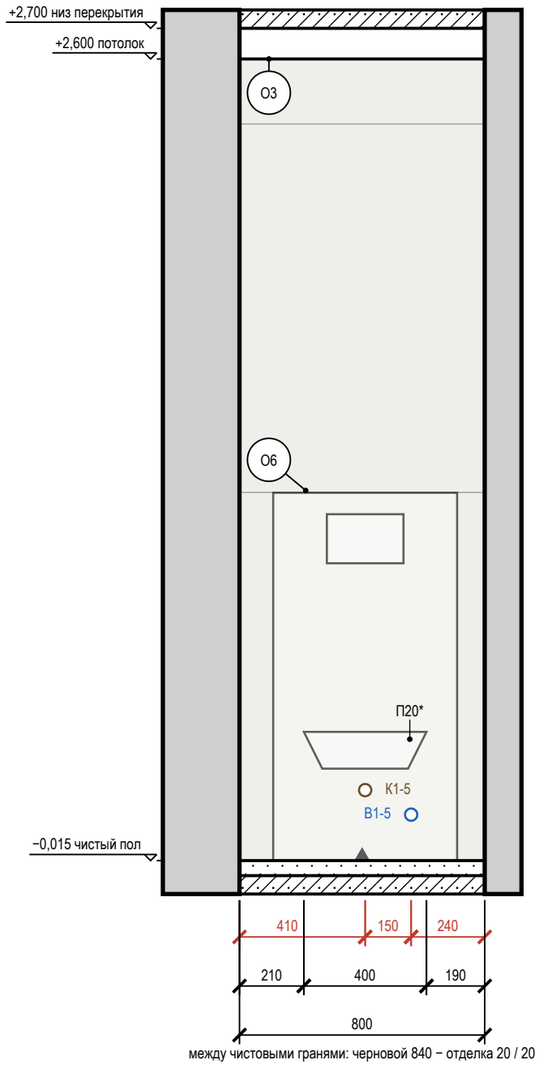

между чистовыми гранями: черновой 840 − отделка 20 / 20

Ведомость точек и выводов

Стена	Марка	Что это	Гр.	Н, мм	От угла, мм	Примечание
Г	К1-5	канализация — унитаз подвесной		230	410	Ø110
Г	В1-5	холодная вода — унитаз подвесной		150	560	в раме инсталляции


Условные обозначения

- вывод В1 (код — в ведомости привязок)
- вывод К1 (код — в ведомости привязок)
- привязки точек и выводов от угла и от пола, мм
- мебель и приборы — фасад по расстановке (условно)
- картина (декор): марка Д, крест — центр, Н — высота центра, мм
- стены и перекрытия в сечении
- плитка: сетка швов по формату, ▲ — ось старта
- О1 — марка отделки по реестру отделки альбома
- А — марка развёртки: буква стены, стрелка — взгляд

Ведомость отделки (на листе)

Марка	Поверхность	Материал, изделие	Цвет, код	Кол.
О3	потолок	окраска, Tikkurila, глубокоматовая	NCS S 0300-N	1,8 м²
О6	стены	облицовка плиткой, Italon Charme Extra, 600×1200 мм, 610015000370	Italon 610015000370 «Charme Extra»	7,6 м²

Схема развёрток (М 1:50)

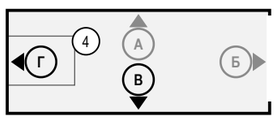

Ведомость изделий и проёмов (на листе)

Стена	Марка	Изделие, проём	На виде Ш×В, мм	Низ, мм
В	ДК9**	картина	300×400	1300
Г	П20*	унитаз подвесной	400×120	300

Примечания

1. Развёртки — вид на стену изнутри помещения, по часовой стрелке; расположение — на схеме листа и на листе 77; размеры — в мм по чистовым поверхностям; отметки — в м от ±0,000; высоты Н — от чистого пола помещения до оси изделия, у декора — до центра.
2. Красная цепочка — привязки электроточек и выводов по осям от угла чистовых стен; высота Н — у знака, от чистого пола до оси; высоты мебели, проёмов и границ отделки — колонкой отметок слева. У знака — короткая марка; назначение, группа щита, высота и привязка каждой точки и вывода — в «Ведомости точек и выводов» под видами (каждая точка — строка).
3. У знака электроточки: марка (Р — розетка, S — выключатель, Св — светильник, ЭВ — вывод кабеля), ×N — число постов в рамке, гр. — группа щита, Н — высота оси от чистого пола, мм; группы по клавишам выключателя — на листе выключателей.
4. Схема мебели, приборов и декора не является технической документацией для производства мебели; габариты — по паспортам изделий (* — высота не задана в проекте, показана по типовому изделию).
5. Облицовка — по сетке швов, раскладка от оси стены (треугольник у пола); подрезки — по листу раскладки плитки.
6. Гидроизоляция в 2 слоя, заход на стены 200 мм — до облицовки, с актом скрытых работ и тестом проливом (узел — на листе узлов).
7. Картины и зеркала крепить к основанию по паспорту изделия (закладные и анкеры — в перечне скрытых работ); крест — ось центра предмета.

Допущения и предложения на листе

Основа листа: размеры сняты с плана заказчика, контрольный обмер не выполнен (К-5); высота потолка 2700 мм принята: на плане заказчика не указана (К-5); подрайон климата не задан — принят не северный (жилые от 2,5 м) (К-4); толщины стен приняты: наружные 250 мм, перегородки 120 мм — не обмерены (К-5); разрешённая мощность 15 кВт принята по типовой квартире, технических условий нет (К-6).

Знак «**» — предложение проектировщика, заказчиком не утверждено (согласовать с заказчиком): ИЗ-4: ДК9.

См. лист открытых вопросов (лист 6, записи К-4–К-6; лист 7, запись ИЗ-4).

1000 мм · печать 1:1

Изм.	Кол.уч	Лист	№ док.	Подп.	Дата
Разраб.		Кырлан А.С.			14.11.26
Пров.					
ГИП					
Н. контр.					
Утв.					

ГД-2026-006-АИ

Квартира 58 м²

Общая площадь 55,23* м² · * размеры приняты, не замерены (реестр — л. 6, 7, К-5)

Дизайн-проект интерьера

Стадия	Лист	Листов
РП	88	108

Развёртки стен В, Г. Санузел (пом. 4)

М 1:20

Кырлан Александр Сергеевич


выпуск 14.11.2026 № bcee049e32 · стр. 97 из 128

Развёртка стены А. Прихожая (пом. 5)

Прихожая (пом. 5) · вид изнутри помещения · размеры в мм, отметки в м

ПРЕДВАРИТЕЛЬНО · не для производства работ · открыто пунктов: 9 (реестр — л. 6, 7)

Стена А (М 1:20)

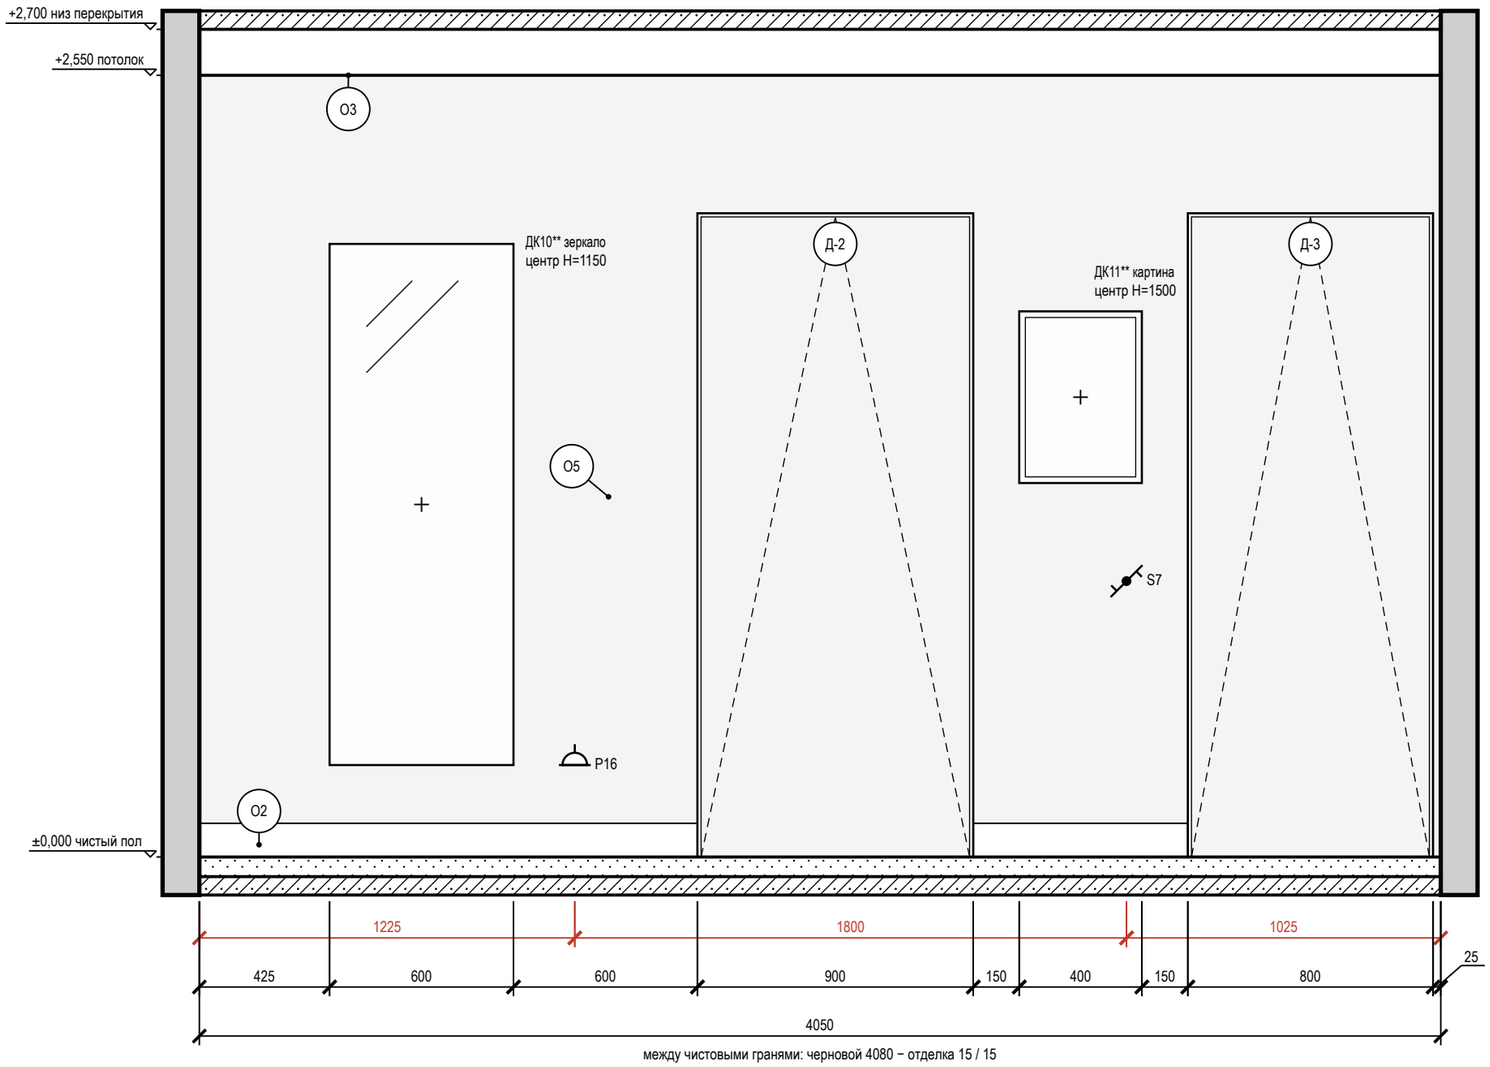

Ведомость точек и выводов

Марка	Что это	Гр.	Н, мм	От угла, мм	Примечание
Р16	розетка: уборка	4	300	1225	
S7	выключатель	1	900	3025	


Условные обозначения

- розетка с заземляющим контактом; у знака марка, ×N — постов в рамке, гр. — группа щита, Н — высота оси, мм
- выключатель одноклавишный
- выключатель с проходной или перекрёстной клавишей (обратный флажок); тип клавиши — в подписи
- привязки точек и выводов от угла и от пола, мм
- мебель и приборы — фасад по расстановке (условно)
- картина (декор): марка Д, крест — центр, Н — высота центра, мм
- зеркало: марка Д, крест — центр, Н — высота центра, мм
- дверь скрытого монтажа: полотно в плоскости стены (узел — на листе узлов)
- стены и перекрытия в сечении
- О1 — марка отделки по реестру отделки альбома
- А — марка развёртки: буква стены, стрелка взгляд

Ведомость отделки (на листе)

Марка	Поверхность	Материал, изделие	Цвет, код	Кол.
О2	плинтус	плинтус МДФ, Orac Decor Luxxus, h 110 мм, SX184, шелковисто-матовая	NCS S 0300-N	2,3 м
О3	потолок	окраска, Tikkurila, глубокоматовая	NCS S 0300-N	9,6 м²
О5	стены	окраска, Tikkurila, шелковисто-матовая, подготовка Q3	NCS S 1502-Y50R	6,8 м²

Схема развёрток (М 1:100)

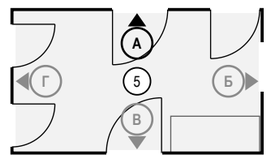

Примечания

1. Развёртки — вид на стену изнутри помещения, по часовой стрелке; расположение — на схеме листа и на листе 77; размеры — в мм по чистовым поверхностям; отметки — в м от ±0,000; высоты Н — от чистого пола помещения до оси изделия, у декора — до центра.
2. Красная цепочка — привязки электроточек и выводов по осям от угла чистовых стен; высота Н — у знака, от чистого пола до оси; высоты мебели, проёмов и границ отделки — колонкой отметок слева. У знака — короткая марка; назначение, группа щита, высота и привязка каждой точки и вывода — в «Ведомости точек и выводов» под видами (каждая точка — строка).
3. У знака электроточки: марка (Р — розетка, S — выключатель, Св — светильник, ЭВ — вывод кабеля), ×N — число постов в рамке, гр. — группа щита, Н — высота оси от чистого пола, мм; группы по клавишам выключателя — на листе выключателей.
4. Схема мебели, приборов и декора не является технической документацией для производства мебели; габариты — по паспортам изделий.
5. Картины и зеркала крепить к основанию по паспорту изделия (закладные и анкеры — в перечне скрытых работ); крест — ось центра предмета.
6. Двери скрытого монтажа — полотно в плоскости стены, отделка стены по полотну, плинтус прерывается у короба (узел — на листе узлов).
7. Потолок — у каждой стены свой, по плану потолков (ПТ1); ступени — зоной, кромка короба перед нишей — тонкой линией; в поле потолка: ПТ2 +2,600.

Допущения и предложения на листе

Основа листа: размеры сняты с плана заказчика, контрольный обмер не выполнен (К-5); высота потолка 2700 мм принята: на плане заказчика не указана (К-5); подрайон климата не задан — принят не северный (жилые от 2,5 м) (К-4); толщины стен приняты: наружные 250 мм, перегородки 120 мм — не обмерены (К-5); разрешённая мощность 15 кВт принята по типовой квартире, технических условий нет (К-6).

Знак «**» — предложение проектировщика, заказчиком не утверждено (согласовать с заказчиком): ИЗ-4: ДК10, ДК11.

См. лист открытых вопросов (лист 6, записи К-4–К-6; лист 7, запись ИЗ-4).

1000 мм · печать 1:1

Изм.	Кол.уч	Лист	№ док.	Подп.	Дата
Разраб.		Кырлан А.С.			14.11.26
Пров.					
ГИП					
Н. контр.					
Утв.					

ГД-2026-006-АИ

Квартира 58 м²

Общая площадь 55,23* м² · * размеры приняты, не замерены (реестр — л. 6, 7, К-5)

Дизайн-проект интерьера

Стадия	Лист	Листов
РП	89	108

Развёртка стены А. Прихожая (пом. 5)

М 1:20

Кырлан Александр Сергеевич


выпуск 14.11.2026 № bcee049e32 · стр. 98 из 128

Развёртки стен Б, Г. Прихожая (пом. 5)

Прихожая (пом. 5) · вид изнутри помещения · размеры в мм, отметки в м


ПРЕДВАРИТЕЛЬНО · не для производства работ · открыто пунктов: 9 (реестр — л. 6, 7)

Стена Б (М 1:25)

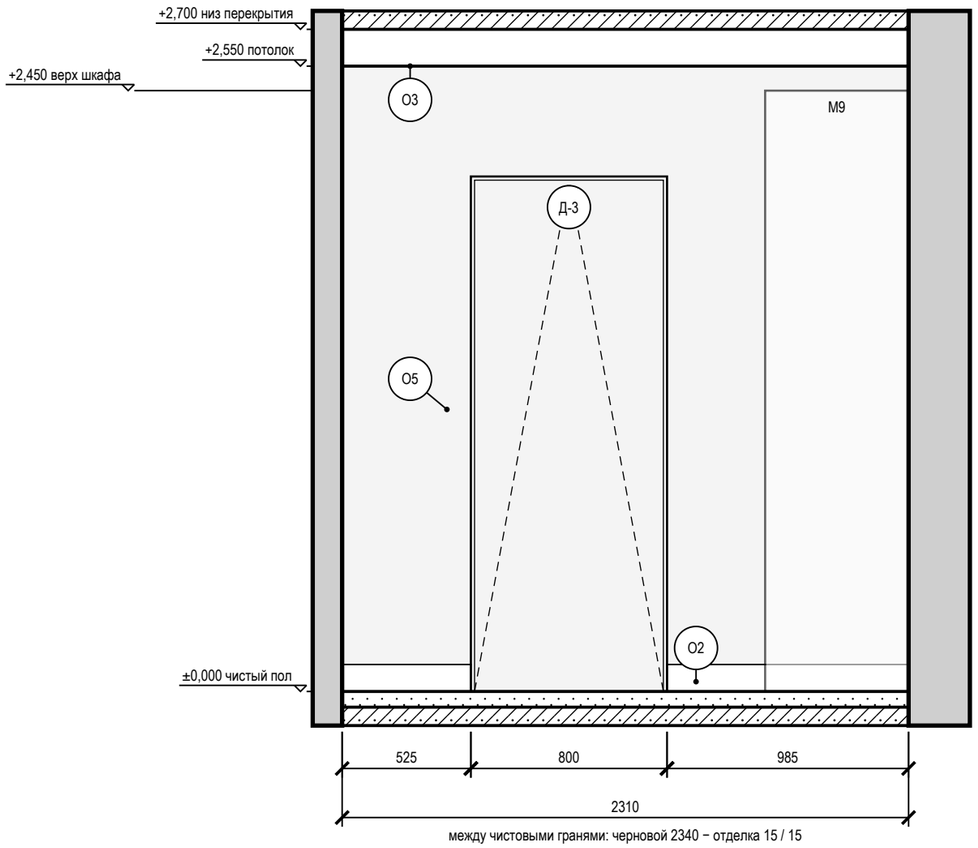

между чистовыми гранями: черновой 2340 − отделка 15 / 15

Стена Г (М 1:25)

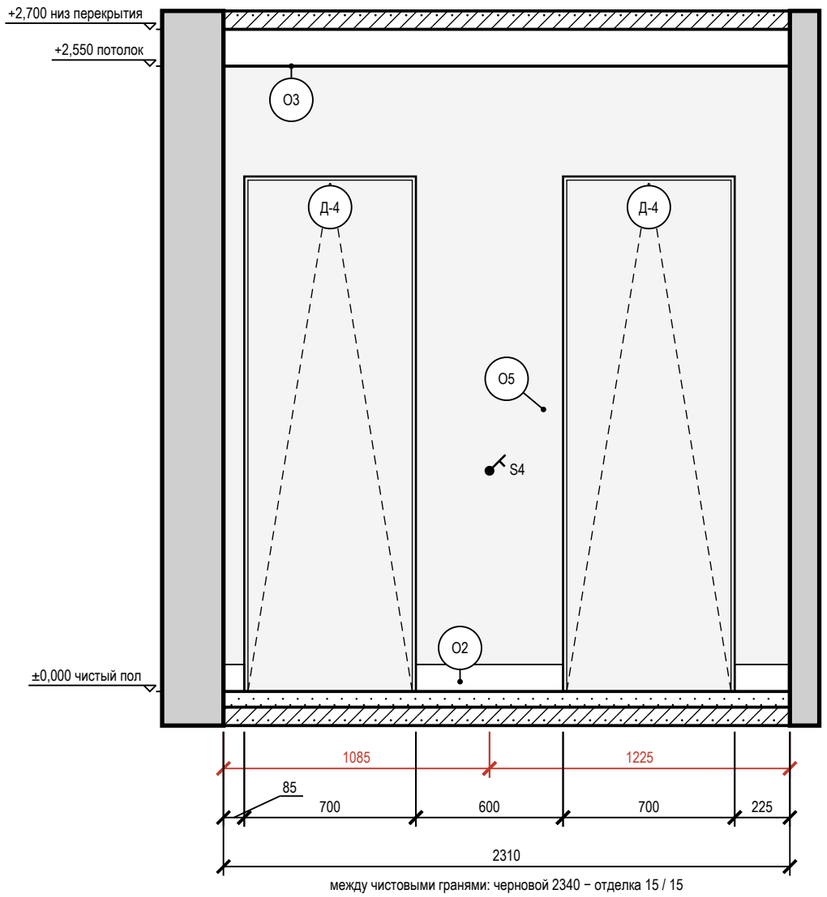


между чистовыми гранями: черновой 2340 − отделка 15 / 15

Условные обозначения

- выключатель одноклавишный
- привязки точек и выводов от угла и от пола, мм
- мебель и приборы — фасад по расстановке (условно)
- дверь скрытого монтажа: полотно в плоскости стены (узел — на листе узлов)
- стены и перекрытия в сечении
- О1 — марка отделки по реестру отделки альбома
- А — марка развёртки: буква стены, стрелка взгляд

Схема развёрток (М 1:100)

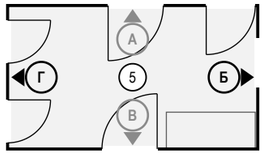

Ведомость точек и выводов

Стена	Марка	Что это	Гр.	Н, мм	От угла, мм	Примечание
Г	S4	выключатель: свет ванной (пом. 3)	1	900	1085	

Ведомость изделий и проёмов (на листе)

Стена	Марка	Изделие, проём	На виде Ш×В, мм	Низ, мм
Б	Д-3	дверь скрытого монтажа	800×2100	0
Б	М9	шкаф-купе	585×2450	0
Г	Д-4	дверь скрытого монтажа	700×2100	0

Примечания

1. Развёртки — вид на стену изнутри помещения, по часовой стрелке; расположение — на схеме листа и на листе 77; размеры — в мм по чистовым поверхностям; отметки — в м от ±0,000; высоты Н — от чистого пола помещения до оси изделия, у декора — до центра.
2. Красная цепочка — привязки электроточек и выводов по осям от угла чистовых стен; высота Н — у знака, от чистого пола до оси; высоты мебели, проёмов и границ отделки — колонкой отметок слева. У знака — короткая марка; назначение, группа щита, высота и привязка каждой точки и вывода — в «Ведомости точек и выводов» под видами (каждая точка — строка).
3. Отделка стен — по ведомости отделки помещений, лист 56.
4. У знака электроточки: марка (Р — розетка, S — выключатель, Св — светильник, ЭВ — вывод кабеля), ×N — число постов в рамке, гр. — группа щита, Н — высота оси от чистого пола, мм; группы по клавишам выключателя — на листе выключателей.
5. Схема мебели, приборов и декора не является технической документацией для производства мебели; габариты — по паспортам изделий.
6. Двери скрытого монтажа — полотно в плоскости стены, отделка стены по полотну, плинтус прерывается у короба (узел — на листе узлов).
7. Потолок — у каждой стены свой, по плану потолков (ПТ1); ступени — зоной, кромка короба перед нишей — тонкой линией; в поле потолка: ПТ2 +2,600.

Допущения и предложения на листе

Основа листа: размеры сняты с плана заказчика, контрольный обмер не выполнен (К-5); высота потолка 2700 мм принята: на плане заказчика не указана (К-5); подрайон климата не задан — принят не северный (жилые от 2,5 м) (К-4); толщины стен приняты: наружные 250 мм, перегородки 120 мм — не обмерены (К-5); разрешённая мощность 15 кВт принята по типовой квартире, технических условий нет (К-6).

См. лист открытых вопросов (лист 6, записи К-4–К-6).

1000 мм · печать 1:1

Изм.	Кол.уч	Лист	№ док.	Подп.	Дата
Разраб.		Кырлан А.С.			14.11.26
Пров.					
ГИП					
Н. контр.					
Утв.					

ГД-2026-006-АИ

Квартира 58 м²

Общая площадь 55,23* м² · * размеры приняты, не замерены (реестр — л. 6, 7, К-5)

Дизайн-проект интерьера

Стадия	Лист	Листов
РП	90	108

Развёртки стен Б, Г. Прихожая (пом. 5)

М 1:25

Кырлан Александр Сергеевич


выпуск 14.11.2026 № bcee049e32 · стр. 99 из 128

Развёртка стены В. Прихожая (пом. 5)

Прихожая (пом. 5) · вид изнутри помещения · размеры в мм, отметки в м

ПРЕДВАРИТЕЛЬНО · не для производства работ · открыто пунктов: 9 (реестр — л. 6, 7)

Стена В (М 1:20)

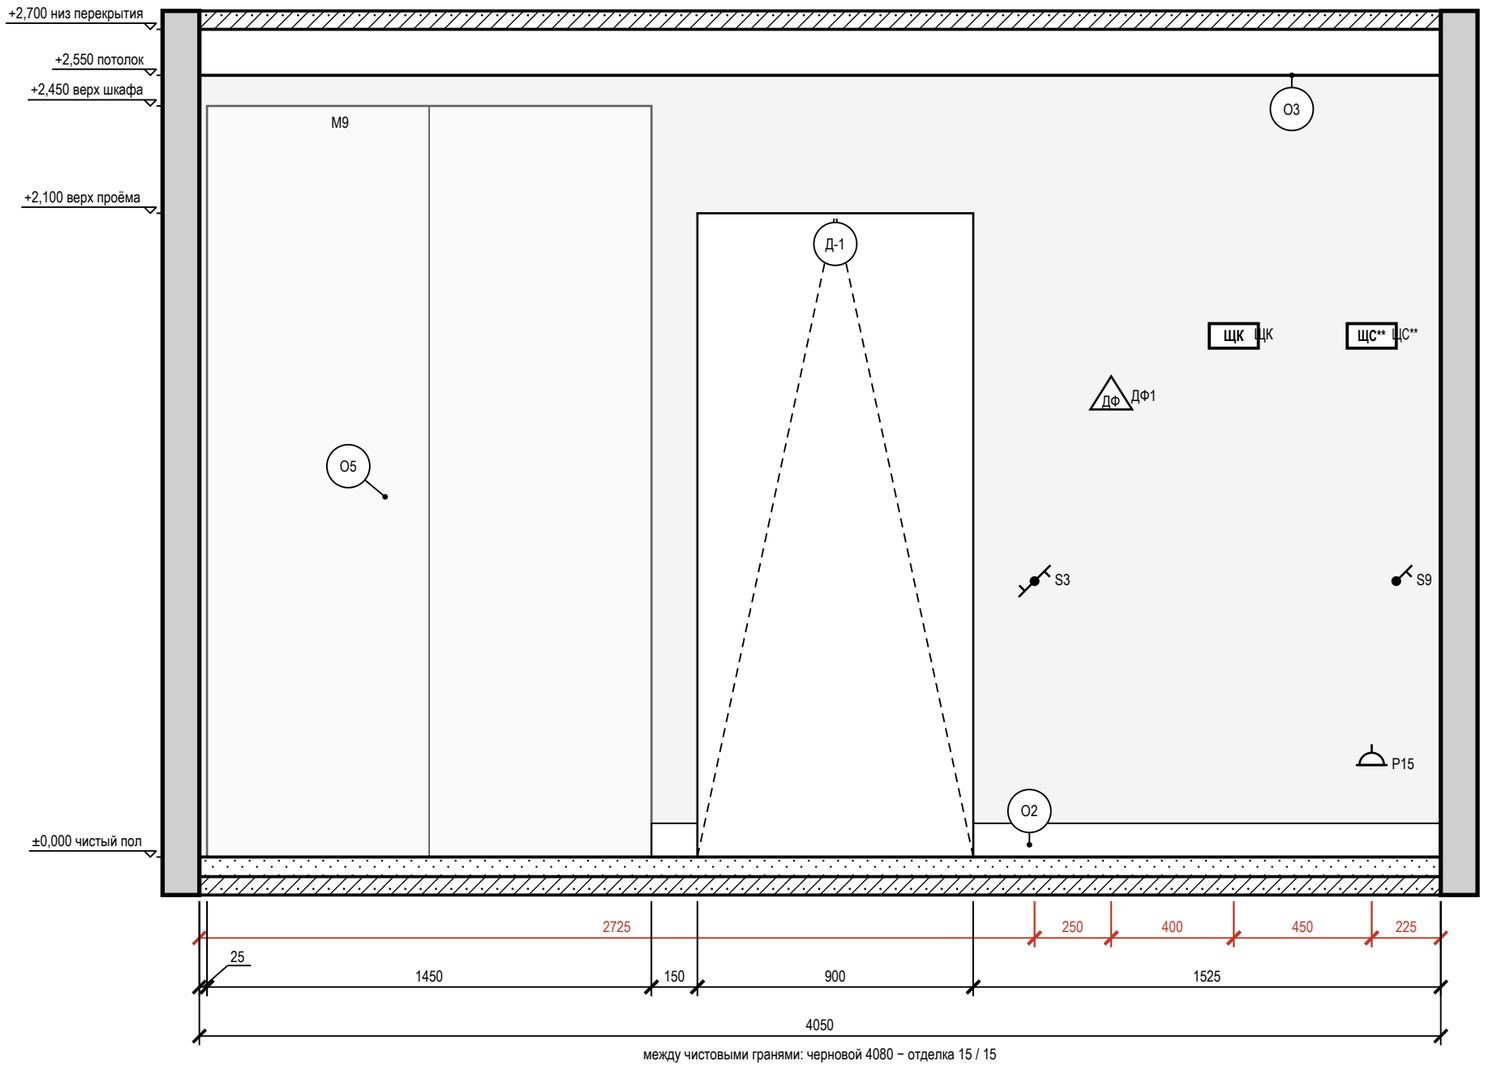

Ведомость точек и выводов

Марка	Что это	Гр.	Н, мм	От угла, мм	Примечание
S3	выключатель	1	900	2725	
ДФ1	домофон: трубка домофона		1500	2975	
ЩК	щит		1700	3375	
Р15	розетка: питание ЩС** (роутер, ИБП)	4	300	3825	
ЩС**	щит: щит слаботочный: ввод провайдера, роутер		1700	3825	
S9	выключатель: свет санузла (пом. 4)	1	900	3905	

Условные обозначения

- розетка с заземляющим контактом; у знака марка, ×N — постов в рамке, гр. — группа щита, Н — высота оси, мм
- выключатель одноклавишный
- выключатель с проходной или перекрёстной клавишей (обратный флажок); тип клавиши — в подписи
- ДФ — трубка или монитор домофона
- ЩК — щит квартирный
- привязки точек и выводов от угла и от пола, мм
- мебель и приборы — фасад по расстановке (условно)
- дверной проём; марка двери — в кружке
- стены и перекрытия в сечении
- О1 — марка отделки по реестру отделки альбома
- А — марка развёртки: буква стены, стрелка взгляд

Ведомость отделки (на листе)

Марка	Поверхность	Материал, изделие	Цвет, код	Кол.
О2	плинтус	плинтус МДФ, Orac Decor Luxxus, h 110 мм, SX184, шелковисто-матовая	NCS S 0300-N	1,7 м
О3	потолок	окраска, Tikkurila, глубокоматовая	NCS S 0300-N	9,6 м²
О5	стены	окраска, Tikkurila, шелковисто-матовая, подготовка Q3	NCS S 1502-Y50R	8,4 м²

Ведомость изделий и проёмов (на листе)

Марка	Изделие, проём	На виде Ш×В, мм	Низ, мм
М9	шкаф-купе	1450×2450	0
Д-1	дверь	900×2100	0

Примечания

1. Развёртки — вид на стену изнутри помещения, по часовой стрелке; расположение — на листе 77; размеры — в мм по чистовым поверхностям; отметки — в м от ±0,000; высоты Н — от чистого пола помещения до оси изделия, у декора — до центра.
2. Красная цепочка — привязки электроточек и выводов по осям от угла чистовых стен; высота Н — у знака, от чистого пола до оси; высоты мебели, проёмов и границ отделки — колонкой отметок слева. У знака — короткая марка; назначение, группа щита, высота и привязка каждой точки и вывода — в «Ведомости точек и выводов» под видами (каждая точка — строка).
3. У знака электроточки: марка (Р — розетка, S — выключатель, Св — светильник, ЭВ — вывод кабеля), ×N — число постов в рамке, гр. — группа щита, Н — высота оси от чистого пола, мм; группы по клавишам выключателя — на листе выключателей.
4. Схема мебели, приборов и декора не является технической документацией для производства мебели; габариты — по паспортам изделий.
5. Потолок — у каждой стены свой, по плану потолков (ПТ1); ступени — зоной, кромка короба перед нишей — тонкой линией; в поле потолка: ПТ2 +2,600.

Допущения и предложения на листе

Основа листа: размеры сняты с плана заказчика, контрольный обмер не выполнен (К-5); высота потолка 2700 мм принята: на плане заказчика не указана (К-5); подрайон климата не задан — принят не северный (жилые от 2,5 м) (К-4); толщины стен приняты: наружные 250 мм, перегородки 120 мм — не обмерены (К-5); разрешённая мощность 15 кВт принята по типовой квартире, технических условий нет (К-6).

Знак «**» — предложение проектировщика, заказчиком не утверждено (согласовать с заказчиком): ЩС — щит слаботочный: место и состав.

См. лист открытых вопросов (лист 6, записи К-4–К-6).

1000 мм · печать 1:1

Изм.	Кол.уч	Лист	№ док.	Подп.	Дата
Разраб.		Кырлан А.С.			14.11.26
Пров.					
ГИП					
Н. контр.					
Утв.					

ГД-2026-006-АИ

Квартира 58 м²

Общая площадь 55,23* м² · * размеры приняты, не замерены (реестр — л. 6, 7, К-5)

Дизайн-проект интерьера

Стадия	Лист	Листов
РП	91	108

Развёртка стены В. Прихожая (пом. 5)

М 1:20

Кырлан Александр Сергеевич


выпуск 14.11.2026 № bcee049e32 · стр. 100 из 128

Развёртка стены А. Гардеробная (пом. 6)

Гардеробная (пом. 6) · вид изнутри помещения · размеры в мм, отметки в м

ПРЕДВАРИТЕЛЬНО · не для производства работ · открыто пунктов: 9 (реестр — л. 6, 7)


Стена А (М 1:20)

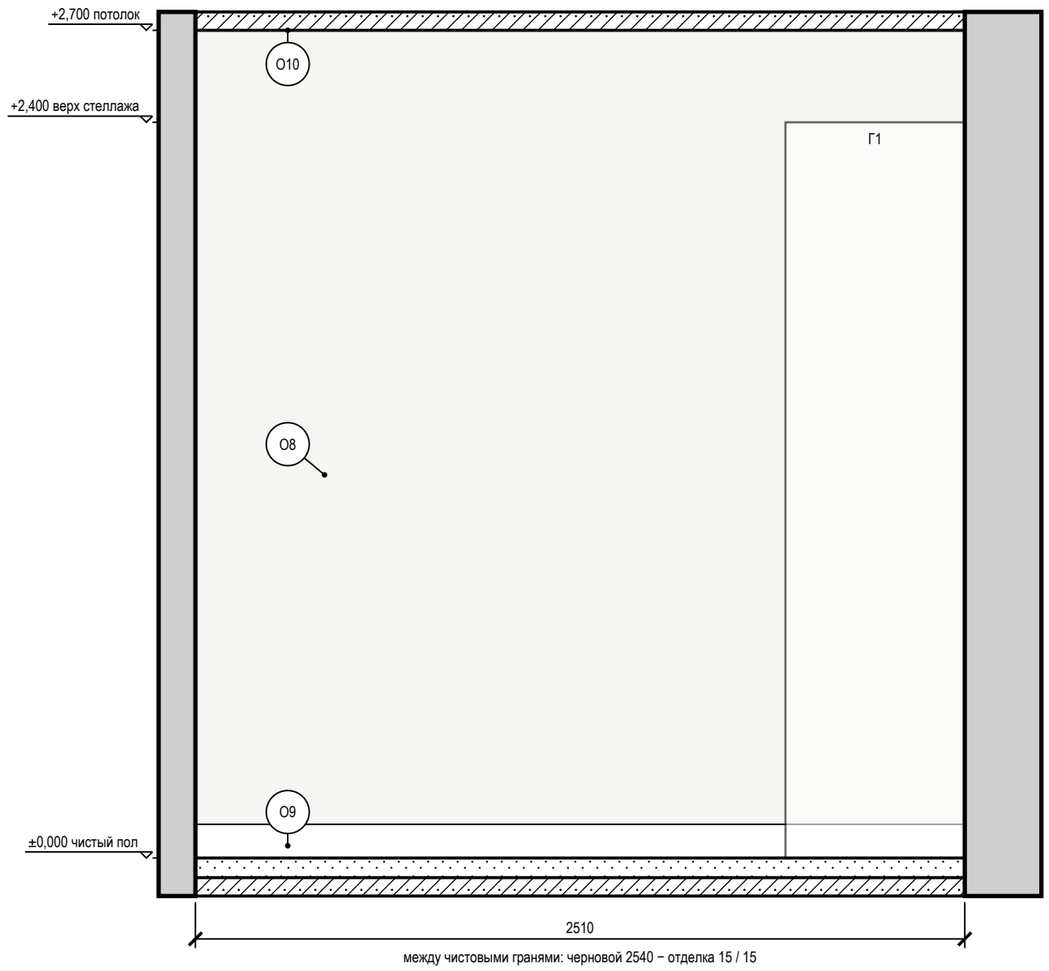

Ведомость отделки (на листе)

Марка	Поверхность	Материал, изделие	Цвет, код	Кол.
О8	стены	окраска, Tikkurila Harmony, матовая, подготовка Q3	Tikkurila V503 «Winter»	6,8 м²
О9	плинтус	плинтус МДФ, Orac Decor Luxxus, h 110 мм, SX184	Tikkurila V503 «Winter»	2,5 м
О10	потолок	окраска, Tikkurila Anti-Reflex 2, глубокоматовая, подготовка Q3	Tikkurila V503 «Winter»	5,9 м²

Схема развёрток (М 1:50)

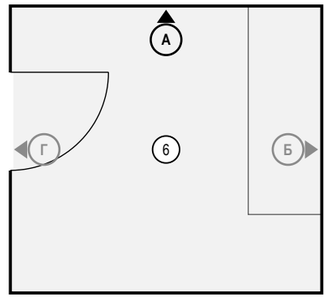

Условные обозначения

- мебель и приборы — фасад по расстановке (условно)
- стены и перекрытия в сечении
- окраска: тон — цвет по коду производителя (условно)
- О1 — марка отделки по реестру отделки альбома
- А — марка развёртки: буква стены, стрелка — взгляд

Ведомость изделий и проёмов (на листе)

Марка	Изделие, проём	На виде Ш×В, мм	Низ, мм
Г1	система хранения: штанги, полки, ящики	585×2400	0

Примечания

1. Развёртки — вид на стену изнутри помещения, по часовой стрелке; расположение — на схеме листа и на листе 77; размеры — в мм по чистовым поверхностям; отметки — в м от ±0,000; высоты Н — от чистого пола помещения до оси изделия, у декора — до центра.
2. Схема мебели, приборов и декора не является технической документацией для производства мебели; габариты — по паспортам изделий.

Допущения и предложения на листе

Основа листа: размеры сняты с плана заказчика, контрольный обмер не выполнен (К-5); высота потолка 2700 мм принята: на плане заказчика не указана (К-5); подрайон климата не задан — принят не северный (жилые от 2,5 м) (К-4); толщины стен приняты: наружные 250 мм, перегородки 120 мм — не обмерены (К-5); разрешённая мощность 15 кВт принята по типовой квартире, технических условий нет (К-6).

См. лист открытых вопросов (лист 6, записи К-4–К-6).

1000 мм · печать 1:1

Изм.	Кол.уч	Лист	№ док.	Подп.	Дата
Разраб.		Кырлан А.С.			14.11.26
Пров.					
ГИП					
Н. контр.					
Утв.					

ГД-2026-006-АИ

Квартира 58 м²

Общая площадь 55,23* м² · * размеры приняты, не замерены (реестр — л. 6, 7, К-5)

Дизайн-проект интерьера

Стадия	Лист	Листов
РП	92	108

Развёртка стены А. Гардеробная (пом. 6)

М 1:20

Кырлан Александр Сергеевич


выпуск 14.11.2026 № bcee049e32 · стр. 101 из 128

Развёртки стен Б, Г. Гардеробная (пом. 6)

Гардеробная (пом. 6) · вид изнутри помещения · размеры в мм, отметки в м


ПРЕДВАРИТЕЛЬНО · не для производства работ · открыто пунктов: 9 (реестр — л. 6, 7)

Стена Б (М 1:25)

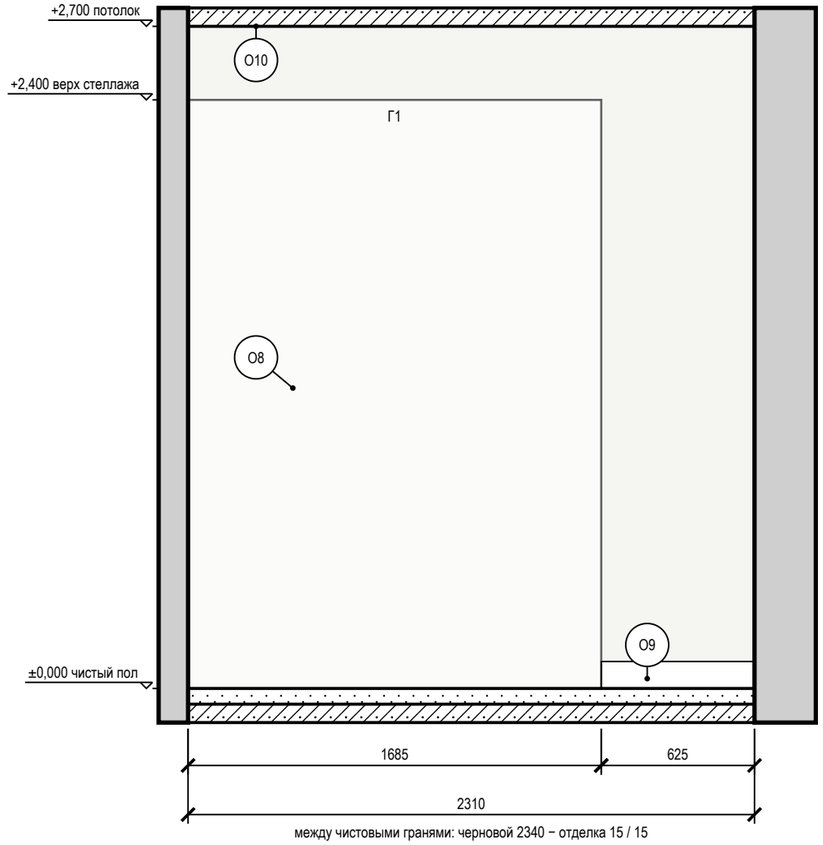

между чистовыми гранями: черновой 2340 − отделка 15 / 15

Стена Г (М 1:25)

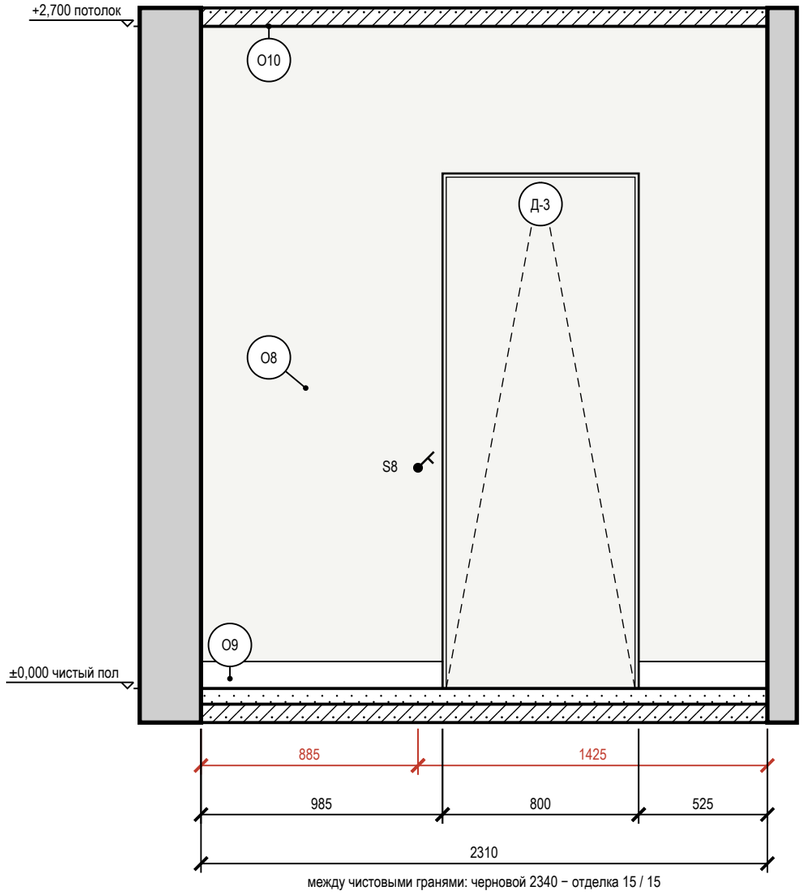


между чистовыми гранями: черновой 2340 − отделка 15 / 15

Условные обозначения

- выключатель одноклавишный
- привязки точек и выводов от угла и от пола, мм
- мебель и приборы — фасад по расстановке (условно)
- дверь скрытого монтажа: полотно в плоскости стены (узел — на листе узлов)
- стены и перекрытия в сечении
- окраска: тон — цвет по коду производителя (условно)
- О1 — марка отделки по реестру отделки альбома
- А — марка развёртки: буква стены, стрелка — взгляд

Схема развёрток (М 1:50)

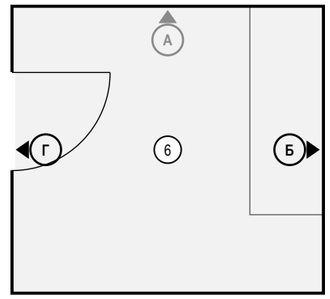

Ведомость точек и выводов

Стена	Марка	Что это	Гр.	Н, мм	От угла, мм	Примечание
Г	S8	выключатель: свет гардеробной	1	900	885	

Ведомость изделий и проёмов (на листе)

Стена	Марка	Изделие, проём	На виде Ш×В, мм	Низ, мм
Б	Г1	система хранения: штанги, полки, ящики	1685×2400	0
Г	Д-3	дверь скрытого монтажа	800×2100	0

Примечания

1. Развёртки — вид на стену изнутри помещения, по часовой стрелке; расположение — на схеме листа и на листе 77; размеры — в мм по чистовым поверхностям; отметки — в м от ±0,000; высоты Н — от чистого пола помещения до оси изделия, у декора — до центра.
2. Красная цепочка — привязки электроточек и выводов по осям от угла чистовых стен; высота Н — у знака, от чистого пола до оси; высоты мебели, проёмов и границ отделки — колонкой отметок слева. У знака — короткая марка; назначение, группа щита, высота и привязка каждой точки и вывода — в «Ведомости точек и выводов» под видами (каждая точка — строка).
3. Отделка стен — по ведомости отделки помещений, лист 56.
4. У знака электроточки: марка (Р — розетка, S — выключатель, Св — светильник, ЭВ — вывод кабеля), ×N — число постов в рамке, гр. — группа щита, Н — высота оси от чистого пола, мм; группы по клавишам выключателя — на листе выключателей.
5. Схема мебели, приборов и декора не является технической документацией для производства мебели; габариты — по паспортам изделий.
6. Двери скрытого монтажа — полотно в плоскости стены, отделка стены по полотну, плинтус прерывается у короба (узел — на листе узлов).

Допущения и предложения на листе

Основа листа: размеры сняты с плана заказчика, контрольный обмер не выполнен (К-5); высота потолка 2700 мм принята: на плане заказчика не указана (К-5); подрайон климата не задан — принят не северный (жилые от 2,5 м) (К-4); толщины стен приняты: наружные 250 мм, перегородки 120 мм — не обмерены (К-5); разрешённая мощность 15 кВт принята по типовой квартире, технических условий нет (К-6).

См. лист открытых вопросов (лист 6, записи К-4–К-6).

1000 мм · печать 1:1

Изм.	Кол.уч	Лист	№ док.	Подп.	Дата
Разраб.		Кырлан А.С.			14.11.26
Пров.					
ГИП					
Н. контр.					
Утв.					

ГД-2026-006-АИ

Квартира 58 м²

Общая площадь 55,23* м² · * размеры приняты, не замерены (реестр — л. 6, 7, К-5)

Дизайн-проект интерьера

Стадия	Лист	Листов
РП	93	108

Развёртки стен Б, Г. Гардеробная (пом. 6)

М 1:25

Кырлан Александр Сергеевич


выпуск 14.11.2026 № bcee049e32 · стр. 102 из 128

Узлы

Пороги и стыки покрытий, скрытые двери, короба стояков, гидроизоляция, плинтус

1 Порог 15 мм: мокрая зона — смежное помещение (М 1:5)


Применение: двери Д-4; места — лист 77

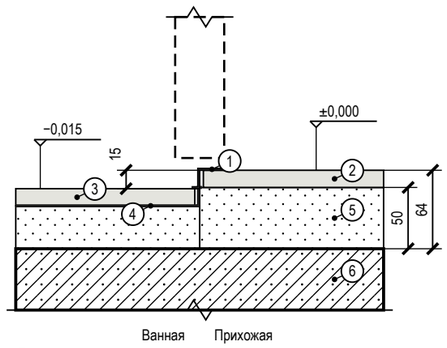

Поз.	Состав слоя, изделие
1	порог-переход металлический, перепад 15 мм, на клей-герметик
2	керамогранит на клею C2 TE S1
3	керамогранит на клею C2 TE S1
4	гидроизоляция в 2 слоя с подъёмом на торец ступени, лента в углу
5	ЦПС М200 50 мм; в мокрой зоне 33 мм
6	плита перекрытия

2 Дверь скрытого монтажа в плоскости стены, плинтус (М 1:5)


Применение: двери Д-2, Д-3, Д-4; места — лист 77

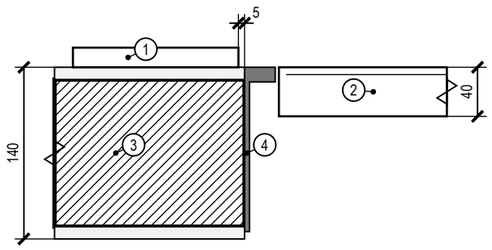

Поз.	Состав слоя, изделие
1	плинтус МДФ 110×16 на клей; у короба — зазор 5 мм, окраска в цвет стены
2	полотно 40 мм под окраску, заподлицо со стеной; теневой шов 3 мм
3	стена 120 мм, штукатурка 10 мм с двух сторон
4	короб скрытого монтажа (алюминий), лицом в плоскости отделки; монтаж до штукатурки

3 Короб стояков К1-1 с люком и звукоизоляцией (М 1:10)


Применение: пом. 3; места — лист 77

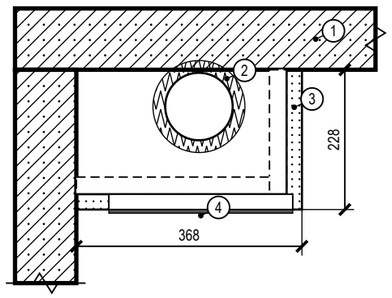

Поз.	Состав слоя, изделие
1	стены существующие — не ослаблять
2	звукоизоляция стояков рулонная 20 мм; К1-1 Ø110
3	короб: профиль 27×28, ГКЛВ 2×12,5 мм, облицовка плиткой
4	ревизионный люк 300×400 мм нажимной, под плитку; против ревизии стояка

4 Гидроизоляция санузла: заход на стены 200 мм, примыкание ванны (М 1:20)


Применение: пом. 3, 4; места — лист 77

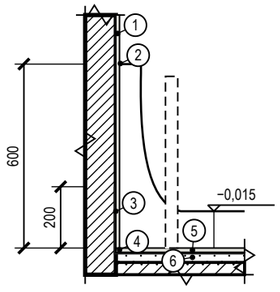

Поз.	Состав слоя, изделие
1	облицовка — плитка на клею C2 TE S1, затирка CG2WA
2	примыкание ванны: лента бордюрная + силиконовый санитарный герметик; облицовка опирается на борт
3	гидроизоляция обмазочная в 2 слоя, заход на стены 200 мм (в зоне душа — выше), до облицовки; акт скрытых работ, тест проливом
4	лента гидроизоляционная в углах и у трапов
5	керамогранит на клею C2 TE S1
6	ЦПС М200 33 мм

5 Плинтус МДФ 110×16 мм у окрашенной стены по доске (ламинату) (М 1:10)


Применение: пом. 1, 2, 6; места — лист 77

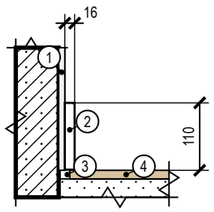

Поз.	Состав слоя, изделие
1	штукатурка, шпаклёвка Q3, окраска — по ведомости отделки
2	плинтус МДФ 110×16 под окраску в цвет стены; клей монтажный — к стене, не к полу
3	зазор покрытия у стены 8–10 мм закрывается плинтусом
4	инженерная доска на клею

6 Плинтус МДФ 110×16 мм у окрашенной стены по керамограниту (плитке) (М 1:10)

Применение: пом. 5; места — лист 77

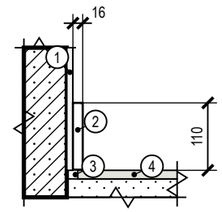

Поз.	Состав слоя, изделие
1	штукатурка, шпаклёвка Q3, окраска — по ведомости отделки
2	плинтус МДФ 110×16 под окраску в цвет стены; клей монтажный — к стене, не к полу
3	зазор покрытия у стены 8–10 мм закрывается плинтусом
4	керамогранит на клею C2 TE S1

Условные обозначения

- железобетон (плита, стены) — условно: конструкция не установлена
- кладка, перегородка — условно: конструкция не установлена
- стяжка, раствор
- гипсокартон ГКЛВ
- звукоизоляция, эластичный заполнитель
- плитка, керамогранит на клею
- инженерная доска (покрытие пола)
- металлический профиль (порог, Т-профиль, короб двери)
- гидроизоляция (обмазочная, лента)

Примечания

1. Узлы — типовые решения проекта для мест, отмеченных выносками на листе схемы расположения развёрток и узлов; размеры — в мм, отметки — в м от ±0,000.
2. Узлы с гидроизоляцией, закладными и коробами скрытого монтажа принимаются по актам скрытых работ до закрытия отделкой; гидроизоляция — после теста проливом (24 ч).
3. Марки изделий (порог, Т-профиль, короб скрытой двери, люк) — по спецификациям; замена — на аналог с теми же габаритами по согласованию с автором проекта.
4. Материал плиты перекрытия и стен в узлах показан условно (железобетон, кладка): конструкция дома не установлена — крепёж, анкеры и толщины слоёв уточняются после обследования (до него — по допущениям общих указаний).

Допущения и предложения на листе. Основа листа: размеры сняты с плана заказчика, контрольный обмер не выполнен (К-5); высота потолка 2700 мм принята: на плане заказчика не указана (К-5); подрайон климата не задан — принят не северный (жилые от 2,5 м) (К-4); толщины стен приняты: наружные 250 мм, перегородки 120 мм — не обмерены (К-5); разрешённая мощность 15 кВт принята по типовой квартире, технических условий нет (К-6). См. лист открытых вопросов (лист 6, записи К-4–К-6).

Изм.	Кол.уч	Лист	№ док.	Подп.	Дата
Разраб.		Кырлан А.С.			14.11.26
Пров.					
ГИП					
Н. контр.					
Утв.					

ГД-2026-006-АИ

Квартира 58 м²

Общая площадь 55,23* м² · * размеры приняты, не замерены (реестр — л. 6, 7, К-5)

Дизайн-проект интерьера

Стадия	Лист	Листов
РП	94	108

Узлы

М 1:5; 1:10; 1:20

Кырлан Александр Сергеевич

выпуск 14.11.2026 № bcee049e32 · стр. 103 из 128

10

Смета

Кырлан Александр Сергеевич

выпуск 14.11.2026 · bcee049e32 · стр. 104 из 128

Ведомость объёмов работ

ПРЕДВАРИТЕЛЬНО · не для производства работ · открыто пунктов: 9 (реестр — л. 6, 7)

Объёмы по помещениям от чертежа · площади в м², длины в м · формула, правило проёмов и источник в каждой строке

Ведомость объёмов работ по помещениям

Поз.	Наименование работ (материал, число слоёв)	Ед. изм.	Объём по помещениям (№ по экспликации)						Всего	Формула подсчёта	Правило проёмов	Источник	Цена за ед., ₽	Стоимость, ₽
			1	2	3	4	5	6						
1. Демонтаж и черновые работы														
1	Демонтаж существующего покрытия пола до основания	м²	21,04	13,95	2,95	1,80	9,55	5,94	55,23	S пом.		л. 20, 21	по КП	
2	Демонтаж существующей отделки стен до основания	м²	41,25	33,91	16,94	14,12	22,66	24,67	153,55	P × H − проёмы	за вычетом проёмов	л. 20, 21	по КП	
3	Демонтаж существующей отделки потолка до основания	м²	21,04	13,95	2,95	1,80	9,55	5,94	55,23	S пом.		л. 20, 21	по КП	
4	Демонтаж существующих дверных блоков	шт					5	1	6	по ведомости проёмов		л. 21, 22	по КП	
5	Демонтаж существующих сантехприборов и электрооборудования (если есть)	компл								по факту на объекте		л. 21	по КП	
6	Устройство стяжки: стяжка ЦПС М200, 50 мм	м²	21,09	14,00	2,99	1,84	9,90	5,99	55,81	S пом. + S в дверных проёмах (b × t/2)	проёмы добавлены	л. 55, 56	530	29 579
7	Гидроизоляция обмазочная, 2 слоя: пол, стены на 200 мм, зоны замачивания	м²			4,22	2,85			7,07	пол + (P − двери) × h заведения + зоны замачивания		л. 51	450	3 182
8	Штукатурка стен по маякам, до 10 мм	м²						24,67	24,67	P × H − проёмы по обводу коробок − грани перегородок на ГКЛВ	за вычетом проёмов	л. 20, 56	530	13 075
9	Штукатурка оконных откосов шириной до 200 мм	м²	1,73	0,86					2,59	Σ (2h + b) × глубина откоса	откосы ≤ 200 мм	л. 20	540	1 399
10	Потолок ГКЛ по каркасу П113, 1 слой	м²	21,04	13,95	2,95	1,80	9,55		49,29	S пом. по плану потолков		л. 48–50	1 500	73 935
Итого по разделу 1 — 121 170 ₽ (позиций 10, из них по КП 5); в сводную смету — л. 100, 101														
2. Инженерные системы														
11	Прокладка слаботочной линии: Кабель домофона — тип по системе поставщика, отдельно от силовых	м							3,40	по лучам от ЩС**: 1 точ., запас 10 %		л. 35	по КП	
12	Прокладка слаботочной линии: Кабель коаксиальный RG-6 (75 Ом) к розеткам ТВ, отдельно от силовых	м							16,30	по лучам от ЩС**: 1 точ., запас 10 %		л. 35	по КП	
13	Прокладка слаботочной линии: Кабель U/UTP кат. 5e (LAN, Wi-Fi и камеры по PoE), отдельно от силовых	м							30,10	по лучам от ЩС**: 2 точ., запас 10 %		л. 35	по КП	
14	Прокладка гофротрубы Ø20 для слаботочных линий, отдельно от силовых	м							44,80	по длине лучей без участков в канале плинтуса (≈ 90 %)		л. 35	140	6 272
15	Сборка слаботочного щита ЩС**: корпус, патч-панель, подключение линий и питания 220 В; коммутатор и точки доступа — оборудование заказчика	шт							1	один щит		л. 31, 35	по КП	
16	Электроточка: подрозетник в бетоне, розетка, выключатель, вывод	шт	16	6	3		7	1	33	по ведомости электроточек		л. 28, 31	950	31 350
17	Штробы в стенах под спуски кабеля к точкам — выполняются только после технического заключения о несущих стенах	м	30,00	11,70	3,35		12,15	1,80	59,00	Σ (H − h) по точкам на стенах: вертикальные спуски	после техзаключения	л. 21, 28	по КП	
18	Установка встраиваемого точечного светильника	шт			1	1	2		4	по плану освещения		л. 29	750	3 000
19	Монтаж светильника: потолочного, подвесного, настенного	шт	2	4	1			1	8	по плану освещения		л. 29	1 200	9 600
20	Монтаж LED-ленты в алюминиевый профиль	м	1,80						1,80	Σ длин лент по плану освещения		л. 29	230	414
21	Установка блока питания LED в доступном месте (люк, шкаф)	шт	1	1					2	один на LED-группу		л. 29	570	1 140
22	Установка автономного пожарного извещателя	шт	1	1			1		3	по плану розеток		л. 28	по КП	
23	Сборка щита: установка автоматов и АВДТ групп, вводного автомата	шт							7	группы + вводной автомат		л. 32	230	1 610
24	Установка вводного УЗО	шт							1	по однолинейной схеме		л. 32	380	380

Допущения и предложения на листе

Основа листа: размеры сняты с плана заказчика, контрольный обмер не выполнен (К-5); высота потолка 2700 мм принята: на плане заказчика не указана (К-5); подрайон климата не задан — принят не северный (жилые от 2,5 м) (К-4); толщины стен приняты: наружные 250 мм, перегородки 120 мм — не обмерены (К-5); разрешённая мощность 15 кВт принята по типовой квартире, технических условий нет (К-6).

Знак «**» — предложение проектировщика, заказчиком не утверждено (согласовать с заказчиком): ЩС — щит слаботочный: место и состав.

См. лист открытых вопросов (лист 6, записи К-4–К-6).

Изм.	Кол.уч	Лист	№ док.	Подп.	Дата
Разраб.		Кырлан А.С.			14.11.26
Пров.					
ГИП					
Н. контр.					
Утв.					

ГД-2026-006-АИ

Квартира 58 м²

Общая площадь 55,23* м² · * размеры приняты, не замерены (реестр — л. 6, 7, К-5)

Дизайн-проект интерьера

Стадия	Лист	Листов
РП	95	108

Ведомость объёмов работ

М б/м

Кырлан Александр Сергеевич

Ведомость объёмов работ (продолжение)

Объёмы по помещениям от чертежа · площади в м², длины в м · формула, правило проёмов и источник в каждой строке

Ведомость объёмов работ по помещениям (продолжение)

Поз.	Наименование работ (материал, число слоёв)	Ед. изм.	Объём по помещениям (№ по экспликации)						Всего	Формула подсчёта	Правило проёмов	Источник	Цена за ед., ₽	Стоимость, ₽
			1	2	3	4	5	6						
25	Монтаж инсталляции, установка подвесного унитаза и кнопки смыва	шт				1			1	по плану выводов		л. 38, 46	10 500	10 500
26	Короб инсталляции: каркас и обшивка ГКЛВ в 2 слоя, ревизионный доступ к смыву	шт				1			1	по плану выводов		л. 38, 51–54	по КП	
27	Короб стояков Ш1 489 × 319 мм (внутренний 436 × 266): каркас и обшивка ГКЛВ в 2 слоя, ревизионный люк 300 × 400	м²			2,11				2,11	свободный периметр короба × Н помещения		л. 20, 38	по КП	
28	Короб К1 над чистым полом: каркас и обшивка ГКЛВ под плитку (материалы — в спецификации ВК)	м.п.	0,40		0,76	0,30			1,46	Σ открытых участков выпусков К1 (профиль листа разводки ВК)		л. 38, 46	по КП	
29	Установка ванны с сифоном	шт			1				1	по плану выводов		л. 38, 46	6 000	6 000
30	Установка умывальника (мойки) с сифоном и смесителем	шт	1		1				2	по плану выводов		л. 38, 46	3 000	6 000
31	Подключение стиральной (посудомоечной) машины к ВК	шт	1						1	по плану выводов		л. 38	по КП	
32	Установка радиатора с узлом подключения и терморегулятором	шт	2	1					3	по плану отопления		л. 37	по КП	
33	Монтаж сплит-системы КВ-1**: внутренний блок на стене, трасса фреона и дренажа до наружного блока, вакуумирование, пусконаладка; наружный блок в корзине на фасаде (высотные работы)	шт	1	1					2	по листу ОВ		л. 36	по КП	
Итого по разделу 2 — 76 266 ₽ (позиций 23, из них по КП 12); в сводную смету — л. 100, 101														
3. Чистовые работы														
34	Облицовка стен керамогранитом 1200×600 на клею	м²			14,95	13,40			28,35	по раскладке: зона облицовки − место за коробом	за вычетом проёмов	л. 51–54	2 500	70 875
35	Облицовка короба инсталляции (ГКЛВ) керамогранитом: лицо, боковины, полка	м²			1,99	1,47			3,46	по раскладке: лицо, боковины, полка		л. 51–54	2 500	8 650
36	Укладка керамогранита на пол, 600×600, на клею	м²			2,99	1,84	9,90		14,73	S пом. + S в дверных проёмах	проёмы добавлены	л. 51–55	1 800	26 514
37	Затирка швов керамогранита	м²			19,89	16,67	9,55		46,11	Σ S облицовки и пола из плитки		л. 51–54	150	6 917
38	Грунтование стен, 2 слоя (под штукатурку и под отделку)	м²	41,25	33,91	16,94	14,12	22,66	24,67	153,55	P × H − проёмы	за вычетом проёмов	л. 56	96	14 741
39	Шпаклёвка стен под окраску, 2 слоя (старт и финиш), уровень Q3	м²	41,25	33,91			22,66	24,67	122,49	P × H − проёмы − фартук	за вычетом проёмов	л. 56	750	91 868
40	Грунтование и шпаклёвка оконных откосов, 2 слоя	м.п.	9,60	4,80					14,40	Σ (2h + b) по окнам	по окнам	л. 20	300	4 320
41	Грунтование потолка, 2 слоя	м²	21,04	13,95	2,95	1,80	9,55	5,94	55,23	S пом.		л. 56	96	5 302
42	Шпаклёвка потолка под окраску, 2 слоя, уровень Q3	м²	21,04	13,95	2,95	1,80	9,55	5,94	55,23	S пом.		л. 48–50, 56	950	52 469
43	Окраска потолка водно-дисперсионной краской, 2 слоя	м²	21,04	13,95	2,95	1,80	9,55	5,94	55,23	S пом.		л. 56	360	19 883
44	Окраска стен водно-дисперсионной краской, 2 слоя	м²	48,26	38,15			32,74	26,35	145,50	P × H − фартук, проёмы не вычитаются	без вычета проёмов	л. 56	300	43 650
45	Окраска оконных откосов, 2 слоя	м.п.	9,60	4,80					14,40	Σ (2h + b) по окнам	по окнам	л. 20	120	1 728
46	Укладка инженерной доски на клей	м²	21,09	14,00				5,99	41,08	S пом. + S в дверных проёмах	проёмы добавлены	л. 55, 56	1 200	49 296
47	Установка плинтуса МДФ h=110 мм	м.п.	17,66	14,16			8,04	8,96	48,82	P − ширина дверных проёмов		л. 56	450	21 969
48	Окраска плинтуса в тоне S 0300-N, 2 слоя	м.п.	17,66	14,16			8,04	8,96	48,82	как плинтус		л. 56	300	14 646
49	Монтаж дверей скрытого монтажа под покраску (поставщик дверей)	шт					4	1	5	по ведомости проёмов		л. 22	5 250	26 250
50	Входная дверь, поставка с монтажом и откосами	шт							1	по ведомости проёмов		л. 22	по КП	
51	Монтаж телевизора М20 на кронштейн, скрытая прокладка HDMI и питания (штроба, трубка), подключение акустики	шт	1						1	по плану расстановки		л. 74	по КП	

Допущения и предложения на листе

Основа листа: размеры сняты с плана заказчика, контрольный обмер не выполнен (К-5); высота потолка 2700 мм принята: на плане заказчика не указана (К-5); подрайон климата не задан — принят не северный (жилые от 2,5 м) (К-4); толщины стен приняты: наружные 250 мм, перегородки 120 мм — не обмерены (К-5); разрешённая мощность 15 кВт принята по типовой квартире, технических условий нет (К-6).

Знак «**» — предложение проектировщика, заказчиком не утверждено (согласовать с заказчиком): ИЗ-3: КВ-1 — длина петли принята по типовому минимуму 3 м; паспорта выбранной модели нет Внутренний блок перенесён со стены А (offset 3300…4200 — внутри оконного проёма 3200…4800) на стену Г, offset 300…1200 (простенок у окна 1, поток вдоль помещения к дивану); наружный блок КН-1 — в простенок между окнами (стена А, 2400…3200).

См. лист открытых вопросов (лист 6, записи К-4–К-6; лист 7, запись ИЗ-3).

Изм.	Кол.уч	Лист	№ док.	Подп.	Дата
Разраб.		Кырлан А.С.			14.11.26
Пров.					
ГИП					
Н. контр.					
Утв.					

ГД-2026-006-АИ

Квартира 58 м²

Общая площадь 55,23* м² · * размеры приняты, не замерены (реестр — л. 6, 7, К-5)

Дизайн-проект интерьера

Стадия	Лист	Листов
РП	96	108

Ведомость объёмов работ (продолжение)

М б/м

Кырлан Александр Сергеевич

Ведомость объёмов работ (окончание)

Объёмы по помещениям от чертежа · площади в м², длины в м · формула, правило проёмов и источник в каждой строке

Ведомость объёмов работ по помещениям (продолжение)

Поз.	Наименование работ (материал, число слоёв)	Ед. изм.	Объём по помещениям (№ по экспликации)						Всего	Формула подсчёта	Правило проёмов	Источник	Цена за ед., ₽	Стоимость, ₽
			1	2	3	4	5	6						
Итого по разделу 3 — 459 078 ₽ (позиций 18, из них по КП 2); в сводную смету — л. 100, 101														

Ведомость подсчёта площадей по помещениям

№	Помещение	S пола, м²	P, м	H, м	P × H, м²	Проёмы, м²	Стены нетто, м²	В дверных проёмах, м²	Плинтус, м	Откосы, м.п.
1	Кухня-гостиная	21,04	18,56	2,60	48,26	7,01	41,25	0,05	17,66	9,60
2	Спальня	13,95	14,96	2,55	38,15	4,24	33,91	0,05	14,16	4,80
3	Ванная	2,95	7,04	2,62	18,41	1,47	16,94	0,04	нет	нет
4	Санузел	1,80	5,96	2,62	15,59	1,47	14,12	0,04	нет	нет
5	Прихожая	9,55	12,84	2,55	32,74	10,08	22,66	0,35	8,04	нет
6	Гардеробная	5,94	9,76	2,70	26,35	1,68	24,67	0,05	8,96	нет
	Итого	**55,23**			**179,49**	**25,95**	**153,54**	**0,58**	**48,82**	**14,40**

Реестр контрольных сумм

Показатель	По ВОР	По чертежу	Расхождение	Лист
Σ площадей помещений без летних, м² — общая площадь по экспликации	55,23	55,23	0,0 %	л. 20
Стены под окраску, м² (шпаклёвка) ведомость отделки	122,49	122,49	0,0 %	л. 56
Потолки под окраску, м² — ведомость отделки	55,23	55,23	0,0 %	л. 56
Плинтус, м — ведомость отделки	48,82	48,82	0,0 %	л. 56
Плитка к заказу, шт — ведомость плитки	152	152	0,0 %	л. 51
Гидроизоляция, м² — ведомость материалов плитки	7,07	12,21	-42,1 %	л. 51
Точки ЭОМ, шт — планы ЭОМ (без щитов)	51	52	-1,9 %	л. 28, 29

Примечания

1. Объёмы — от геометрии проекта (та же, что на планах и в ведомости отделки), не от общей площади: P — периметр чистого контура, H — от чистого пола до низа потолка, проёмы — по наружному обводу коробок.
2. Подсчёт по ГЭСН-2001-15 и ГЭСН-2001-11: штукатурка и шпаклёвка стен — за вычетом проёмов; окраска водными составами — без вычета проёмов (п. 2.24); откосы — отдельно, по ширине до 200 и более 200 мм; полы — с площадью в дверных проёмах.
3. Плитка — по раскладке (целые и с подрезкой); короб инсталляции и фартук — отдельными строками, двойного счёта облицовки нет. Материалы, запас и количество к заказу — в спецификации материалов.
4. Цены — ориентир по открытым прайсам Москвы (прайсы собраны 21.09.2026, часть расценок сверена повторно 08.11.2026), не коммерческое предложение; «по КП» — расценки нет, строка в итог не входит.
5. Демонтаж — по плану демонтажа и общим указаниям: покрытия пола, отделка стен и потолков, дверные блоки — до основания; объёмы справочные — по плану демонтажа (расценки в книге нет — «по КП»).
6. Штробы в стенах — только после технического заключения о несущих стенах (общие указания, план обмера и демонтажа): строка «Штробы в стенах» вертикальные спуски кабеля от потолочной трассы к точкам, объём не меньше фактического (горизонтальные трассы — по исполнительной схеме). Расценки штробления в прайсе нет — «по КП», в итог не входит; кабель в штробах стен прокладывается после неё.
7. Слаботочные сети: кабель по лучам от ЩС** 49,80 м (U/UTP, RG-6, домофон — по видам), гофра 44,80 м, щит ЩС** с патч-панелью; розетки RJ45 и ТВ монтируются в строке «Электроточка». Длины те же, что в ведомости изделий электрика (одна модель — lowcurrent-engineer/bom.js); оборудование заказчика (точки доступа, камеры, коммутатор) в спецификацию не входит.
8. Коробы: стояков (Ш1 — 2,11 м²) и К1 над чистым полом (1,45 м открытых участков; труба К1 вдоль стен 11,22 м в короб не зашивается — она за приборами, в раме инсталляции и в шахтах). В спецификации ВК короб К1 заказывается с запасом 10 % — 1,60 м. Материалы коробов стояков и инсталляции — в спецификации материалов, К1 — в спецификации ВК.

Допущения и предложения на листе

Основа листа: размеры сняты с плана заказчика, контрольный обмер не выполнен (К-5); высота потолка 2700 мм принята: на плане заказчика не указана (К-5); подрайон климата не задан — принят не северный (жилые от 2,5 м) (К-4); толщины стен приняты: наружные 250 мм, перегородки 120 мм — не обмерены (К-5); разрешённая мощность 15 кВт принята по типовой квартире, технических условий нет (К-6).

Знак «**» — предложение проектировщика, заказчиком не утверждено (согласовать с заказчиком): ЩС — щит слаботочный: место и состав.

См. лист открытых вопросов (лист 6, записи К-4–К-6).

Изм.	Кол.уч	Лист	№ док.	Подп.	Дата
Разраб.		Кырлан А.С.			14.11.26
Пров.					
ГИП					
Н. контр.					
Утв.					

ГД-2026-006-АИ

Квартира 58 м²

Общая площадь 55,23* м² · * размеры приняты, не замерены (реестр — л. 6, 7, К-5)

Дизайн-проект интерьера

Стадия	Лист	Листов
РП	97	108

Ведомость объёмов работ (окончание)

М б/м

Кырлан Александр Сергеевич

Спецификация материалов

Отделочные материалы: чистое количество, запас, упаковка, к заказу · ГОСТ 21.110-2013

ПРЕДВАРИТЕЛЬНО · не для производства работ · открыто пунктов: 9 (реестр — л. 6, 7)

Спецификация материалов (ГОСТ 21.110-2013, форма 1)

Поз.	Наименование и техническая характеристика	Тип, марка, артикул	Код продукции	Поставщик	Ед. изм.	Количество				Масса ед., кг	Примечание
						чистое	запас, %	упаковка	к заказу		
Покрытия полов и облицовка											
1	Инженерная доска (дуб натуральный, рабочий слой 4 мм, эмиссия E1, прямая укладка)	аналог: инженерная доска, дуб натуральный, масло, 1-полосная, 14/4 мм			м²	41,08	7	по артикулу	44,00 м²		пом. 1, 2, 6; до целой упаковки; л. 55, 56
2	Клей для паркетной и инженерной доски (эластичный, по ТУ изготовителя доски)	по выбору подрядчика			м²	41,08		ведро по ТУ	по ТУ		расход кг/м² — по ТУ клея; л. 55
3	Керамогранит 600×600 мм SG651622R	SG651622R			шт	48	10	коробка	54 шт		12 целых + 36 с подрезкой; 14,30 м² по раскладке, к заказу 19,44 м²; пом. 3, 4, 5; л. 51–54
4	Керамогранит 1200×600 мм 610015000370	610015000370			шт	87	10	коробка	98 шт		0 целых + 87 с подрезкой; 31,81 м² по раскладке, к заказу 70,56 м²; пом. 3, 4; л. 51–54
Сухие смеси и гидроизоляция											
5	Клей плиточный цементный класса C2 S1 (ГОСТ Р 56387-2018)	по выбору подрядчика			кг	24,94	10	мешок 25 кг	2 меш.	25	слой 5 мм, 1,20 кг/м² на 1 мм; л. 51
6	Клей плиточный цементный класса C2 (ГОСТ Р 56387-2018)	по выбору подрядчика			кг	240,94	10	мешок 25 кг	11 меш.	25	слой 5 мм, 1,20 кг/м² на 1 мм; л. 51
7	Затирка цементная класса класс не задан, цвет — по колерной карте	по выбору подрядчика			кг	3,51	10	упак. 2 кг	2 упак.	2	расход (a+b)/ab × шов × t × 1,6 кг/м²; л. 51
8	Гидроизоляция обмазочная полимерная, 2 слоя, лента в углах, манжеты на выводах	по выбору подрядчика			м²	7,07	10	ведро по ТУ	по ТУ		пом. 3, 4; расход кг/м² — по ТУ; л. 51
9	Лента демпферная по периметру пола из плитки	по выбору подрядчика			м	19,14	10	рулон	22,00 м		л. 51
10	Смесь цементно-песчаная для стяжки М200 (50 мм, 33 мм)	по выбору подрядчика			м³	2,71	5	мешок по ТУ	по ТУ		S 55,81 м² × толщина; армирование и маяки — по ТУ; л. 55
11	Смесь штукатурная гипсовая для машинного и ручного нанесения по маякам, слой до 10 мм	по выбору подрядчика			м²	24,67	10	мешок по ТУ	по ТУ		пом. 6; расход кг/м² на 1 мм слоя — по ТУ смеси, толщина — по замеру кривизны стен; л. 20, 56
Короба из ГКЛВ											
12	Лист ГКЛВ 12,5 мм, 2500 × 1200 мм, обшивка коробов в 2 слоя	по выбору подрядчика			м²	4,22	10	лист 3,00 м²	2,00 лист		короб Ш1 пом. 3: 2,11 м²; площадь × 2 слоя; короб К1 над полом — в спецификации ВК; л. 38, 51–54
13	Профиль стальной оцинкованный 27 × 28 мм: каркас коробов (стойки и направляющие)	по выбору подрядчика			м	12,08	10	хлыст 3 м	5 шт		стойки через 400 мм по свободному периметру + направляющие по полу и потолку; крепёж, лента, шпаклёвка швов — по узлу короба; л. 38, 51–54
Слаботочные сети											
14	Кабель домофона — тип по системе поставщика	по выбору подрядчика			м	3,40		бухта по ТУ	4,00 м		по лучам от ЩС**, 1 точ., запас 10 % уже в длине; л. 35
15	Кабель коаксиальный RG-6 (75 Ом) к розеткам ТВ	по выбору подрядчика			м	16,30		бухта по ТУ	17,00 м		по лучам от ЩС**, 1 точ., запас 10 % уже в длине; л. 35
16	Кабель U/UTP кат. 5e (LAN, Wi-Fi и камеры по PoE)	по выбору подрядчика			м	30,10		бухта по ТУ	31,00 м		по лучам от ЩС**, 2 точ., запас 10 % уже в длине; л. 35
17	Гофротруба Ø20 для слаботочных линий, отдельно от силовых	по выбору подрядчика			м	44,80		бухта по ТУ	45,00 м		по длине лучей без участков в канале плинтуса (≈ 90 %); л. 35
18	Розетка компьютерная RJ45, кат. 6, с рамкой и подрозетником	по выбору подрядчика			шт	2		шт	2 шт		LAN1, LAN2; серия механизмов — как у розеток и выключателей; л. 31, 35

Допущения и предложения на листе

Основа листа: размеры сняты с плана заказчика, контрольный обмер не выполнен (К-5); высота потолка 2700 мм принята: на плане заказчика не указана (К-5); подрайон климата не задан — принят не северный (жилые от 2,5 м) (К-4); толщины стен приняты: наружные 250 мм, перегородки 120 мм — не обмерены (К-5); разрешённая мощность 15 кВт принята по типовой квартире, технических условий нет (К-6).

Знак «**» — предложение проектировщика, заказчиком не утверждено (согласовать с заказчиком): ЩС — щит слаботочный: место и состав; пол пом. 1, 2, 6 — артикул изделия не выбран: позиция описана характеристиками («аналог по характеристикам»), артикул выбирается при закупке.

См. лист открытых вопросов (лист 6, записи К-4–К-6).

Изм.	Кол.уч	Лист	№ док.	Подп.	Дата
Разраб.		Кырлан А.С.			14.11.26
Пров.					
ГИП					
Н. контр.					
Утв.					

ГД-2026-006-АИ

Квартира 58 м²

Общая площадь 55,23* м² · * размеры приняты, не замерены (реестр — л. 6, 7, К-5)

Дизайн-проект интерьера

Стадия	Лист	Листов
РП	98	108

Спецификация материалов

М б/м

Кырлан Александр Сергеевич

Спецификация материалов (окончание)

Отделочные материалы: чистое количество, запас, упаковка, к заказу · ГОСТ 21.110-2013

Спецификация материалов (ГОСТ 21.110-2013, форма 1) (продолжение)

Поз.	Наименование и техническая характеристика	Тип, марка, артикул	Код продукции	Поставщик	Ед. изм.	Количество				Масса ед., кг	Примечание
						чистое	запас, %	упаковка	к заказу		
19	Розетка телевизионная (коаксиальная) с рамкой и подрозетником	по выбору подрядчика			шт	1		шт	1 шт		ТВ1; серия механизмов — как у розеток и выключателей; л. 31, 35
20	Трубка или монитор домофона (поставка домофонной организации)	по выбору подрядчика			шт	1		шт	1 шт		ДФ1; серия механизмов — как у розеток и выключателей; л. 31, 35
21	Щит слаботочный ЩС**: корпус, DIN-рейка, розетки 220 В	по выбору подрядчика			шт	1		шт	1 шт		ЩС**; серия механизмов — как у розеток и выключателей; л. 31, 35
22	Патч-панель, портов не менее 2	по выбору подрядчика			шт	1		шт	1 шт		серия механизмов — как у розеток и выключателей; л. 31, 35
Лакокрасочные материалы											
23	Краска интерьерная акриловая, полуматовая, класс истирания 1	Tikkurila S 1002-Y50R			л	9,90	10	банка 2,7 л	5 банк		41,25 м² × 2 сл. × 0,12 л/м²; пом. 1; л. 56
24	Краска интерьерная водно-дисперсионная, глубокоматовая, класс истирания 1	Tikkurila S 0300-N			л	11,83	10	банка 2,7 л	5 банк		49,29 м² × 2 сл. × 0,12 л/м²; пом. 1 (пот.), 2 (пот.), 3 (пот.), 4 (пот.), 5 (пот.); л. 56
25	Краска интерьерная акриловая, глубокоматовая, класс истирания 2	Tikkurila S 1502-Y50R			л	8,14	10	банка 2,7 л	4 банк		33,91 м² × 2 сл. × 0,12 л/м²; пом. 2; л. 56
26	Краска интерьерная акриловая, полуматовая, класс истирания 1	Tikkurila S 1502-Y50R			л	5,44	10	банка 2,7 л	3 банк		22,66 м² × 2 сл. × 0,12 л/м²; пом. 5; л. 56
27	Краска интерьерная акриловая, матовая, класс истирания 1	Tikkurila Harmony V503 «Winter»			л	5,92	10	банка 2,7 л	3 банк		24,67 м² × 2 сл. × 0,12 л/м²; пом. 6; л. 56
28	Краска интерьерная акриловая, глубокоматовая, класс истирания 2	Tikkurila Anti-Reflex 2 V503 «Winter»			л	1,43	10	банка 2,7 л	1 банк		5,94 м² × 2 сл. × 0,12 л/м²; пом. 6 (пот.); л. 56
29	Шпаклёвка финишная полимерная под окраску (стены и потолки, Q3)	по выбору подрядчика			м²	177,72	10	ведро по ТУ	по ТУ		расход кг/м² на слой — по ТУ; л. 56
30	Грунтовка акриловая глубокого проникновения, 2 слоя	по выбору подрядчика			м²	208,78	10	канистра по ТУ	по ТУ		расход л/м² — по ТУ; л. 56
Погонажные изделия и потолки											
31	Плинтус напольный МДФ под покраску, h=110 мм, крепление к стене	SX184			м.п.	48,82	10	хлыст 2,4 м	23 шт		пом. 1, 2, 5, 6; длина хлыста — по артикулу; л. 56
32	Потолок подвесной ГКЛ/ГКЛВ по каркасу Knauf П113: листы, профили, подвесы, лента, шпаклёвка швов	Knauf П113			м²	49,29		комплект	по л. потолков		площадь — по ведомости потолков; число листов, профилей и подвесов — по шагам каркаса на листе потолков; л. 48–50

Примечания

1. Чистое количество — из ведомости объёмов работ и раскладки плитки; запас — отдельной графой (доска — по ведомости отделки, плитка, краска и плинтус — 10 %); «к заказу» — с запасом и кратно упаковке.
2. Плитка — штуками по раскладке, запас на каждую поверхность. Калибр (рабочий размер) и тон — одной партией на помещение, калибр указать при заказе и сверить с раскладкой до укладки.
3. Краска — 0,12 л/м² на слой (середина вилки 0,10–0,15 л/м²) по фактической площади окраски из ведомости отделки; колеровка одной партией.
4. «По ТУ» — расход задаёт производитель выбранного продукта; количество к заказу — после выбора марки.
5. Поз. 1 заданы характеристиками («аналог:»): марку, артикул и поставщика согласовать с заказчиком до закупки, без артикула не заказывать.
6. Штукатурная смесь — на ту же площадь, что строка ВОР «Штукатурка стен» (24,67 м²): площадь одна, расход смеси задаёт производитель.
7. Коробы инсталляции и стояков: ГКЛВ в 2 слоя и профиль 27 × 28 мм считаются по свободным граням коробов (источник — раскладка плиточника и шахты в данных); короб К1 над полом — в спецификации ВК.
8. Потолки ГКЛ: в этой спецификации — площадь системы П113; число листов, профилей и подвесов — по шагам каркаса на листе потолков (подвесы через 1000, несущие через 500, основные через 1200 мм), схема каркаса не выпущена. Сантехника, светильники и мебель — по своим спецификациям.

Допущения и предложения на листе

Основа листа: размеры сняты с плана заказчика, контрольный обмер не выполнен (К-5); высота потолка 2700 мм принята: на плане заказчика не указана (К-5); подрайон климата не задан — принят не северный (жилые от 2,5 м) (К-4); толщины стен приняты: наружные 250 мм, перегородки 120 мм — не обмерены (К-5); разрешённая мощность 15 кВт принята по типовой квартире, технических условий нет (К-6).

Знак «**» — предложение проектировщика, заказчиком не утверждено (согласовать с заказчиком): ЩС — щит слаботочный: место и состав; пол пом. 1, 2, 6 — артикул изделия не выбран: позиция описана характеристиками («аналог по характеристикам»), артикул выбирается при закупке.

См. лист открытых вопросов (лист 6, записи К-4–К-6).

Изм.	Кол.уч	Лист	№ док.	Подп.	Дата
Разраб.		Кырлан А.С.			14.11.26
Пров.					
ГИП					
Н. контр.					
Утв.					

ГД-2026-006-АИ

Квартира 58 м²

Общая площадь 55,23* м² · * размеры приняты, не замерены (реестр — л. 6, 7, К-5)

Дизайн-проект интерьера

Стадия	Лист	Листов
РП	99	108

Спецификация материалов (окончание)

М б/м

Кырлан Александр Сергеевич

Смета ориентировочная

ПРЕДВАРИТЕЛЬНО · не для производства работ · открыто пунктов: 9 (реестр — л. 6, 7)

Работы, материалы, оборудование, услуги и резерв · цены — ориентир по открытым прайсам, не коммерческое предложение

Сводная смета (прайсы собраны 21.09.2026, часть расценок сверена повторно 08.11.2026, Москва)

№	Наименование работ, материалов, услуг	Ед. изм.	Кол-во	Цена за ед., ₽	Стоимость, ₽			Чей подряд	Срок поставки, дн.	Основание	Источник цены
					план	факт	разница				
Работы — по ведомости объёмов работ											
1	Демонтаж и черновые работы (без 5 поз. по КП)	раздел	1		121 170			бригада		ВОР, поз. 1–10; л. 95–97	по ВОР
2	Инженерные системы (без 12 поз. по КП)	раздел	1		76 266			бригада		ВОР, поз. 11–33; л. 95–97	по ВОР
3	Чистовые работы (без 2 поз. по КП)	раздел	1		459 078			бригада, поставщик		ВОР, поз. 34–51; л. 95–97	по ВОР
Материалы — по спецификации материалов											
4	Инженерная доска	м²	44,00	4 513	198 572			поставщик		спецификация, поз. 1	Ц7
5	Керамогранит 600×600 мм	м²	19,44	1 800	34 992			поставщик		спецификация, поз. 3	Ц6
6	Керамогранит 1200×600 мм	м²	70,56	3 500	246 960			поставщик		спецификация, поз. 4	Ц6
7	Клей плиточный цементный класса C2 S1	меш.	13	1 800	23 400			поставщик		спецификация, поз. 5, 6	Ц7
8	Краска Tikkurila (Harmony, Anti-Reflex 2), банка 2,7 л	банк	21	3 510	73 710			поставщик		спецификация, поз. 23, 24, 25, 26, 27, 28	Ц6
9	Плинтус напольный МДФ под покраску	шт	23	368	8 464			поставщик		спецификация, поз. 31	Ц7
10	Прочие материалы с расходом по ТУ (клей для доски, затирка, гидроизоляция, демпферная лента, смесь для стяжки, смесь штукатурная гипсовая для машинного и ручного нанесения по маякам, лист гклв 12, профиль стальной оцинкованный 27 × 28 мм: каркас коробов (стойки и направляющие), кабель слаботочки, гофра слаботочки, изделия слаботочки, шпаклёвка, грунтовка, каркас и ГКЛ потолков)	компл	1	по КП				поставщик		спецификация, поз. 2, 7, 8, 9, 10, 11, 12, 13, 14, 15, 16, 17, 18, 19, 20, 21, 22, 29, 30, 32	
Оборудование и мебель — поставка по спецификациям											
11	Кухонный гарнитур по проекту кухни, изготовление и монтаж (4–8 нед.)	компл	1	по КП				поставщик	не задан; ориентир 4–8 нед. от замера	л. 69–71	
12	Двери скрытого монтажа с коробом под покраску, поставка	шт	5	по КП				поставщик	не задан; ориентир ≈ 30 дн.	л. 22	

Допущения и предложения на листе

Основа листа: размеры сняты с плана заказчика, контрольный обмер не выполнен (К-5); высота потолка 2700 мм принята: на плане заказчика не указана (К-5); подрайон климата не задан — принят не северный (жилые от 2,5 м) (К-4); толщины стен приняты: наружные 250 мм, перегородки 120 мм — не обмерены (К-5); разрешённая мощность 15 кВт принята по типовой квартире, технических условий нет (К-6).

См. лист открытых вопросов (лист 6, записи К-4–К-6).

Изм.	Кол.уч	Лист	№ док.	Подп.	Дата
Разраб.		Кырлан А.С.			14.11.26
Пров.					
ГИП					
Н. контр.					
Утв.					

ГД-2026-006-АИ

Квартира 58 м²

Общая площадь 55,23* м² · * размеры приняты, не замерены (реестр — л. 6, 7, К-5)

Дизайн-проект интерьера

Стадия	Лист	Листов
РП	100	108

Смета ориентировочная

М б/м

Кырлан Александр Сергеевич

Смета ориентировочная (окончание)

Работы, материалы, оборудование, услуги и резерв · цены — ориентир по открытым прайсам, не коммерческое предложение

Сводная смета (прайсы собраны 21.09.2026, часть расценок сверена повторно 08.11.2026, Москва) (продолжение)

№	Наименование работ, материалов, услуг	Ед. изм.	Кол-во	Цена за ед., ₽	Стоимость, ₽			Чей подряд	Срок поставки, дн.	Основание	Источник цены
					план	факт	разница				
13	Оборудование заказчика слаботочных сетей: коммутатор — 1 шт	компл	1	по КП				заказчик		л. 31	
14	Сантехника, светильники, мебель и предметы интерьера	компл	1	по КП				поставщик		л. 46; л. 47; л. 74; л. 25–27	
Прочие работы и услуги											
15	Вынос и вывоз строительного мусора	м³		по факту				бригада		после демонтажа	
16	Подъём материалов на этаж (лифтом или вручную — по договору)	т		по факту				бригада		по массе поставки	
17	Доставка чистовых материалов, 10 % от поставки			10 %	58 610			поставщик		от суммы материалов	
18	Уборка после ремонта	м²	55,23	по факту				бригада		S квартиры	
	Итого работы				**656 514**						
	Итого материалы				**586 098**						
	Итого прочие услуги				**58 610**						
	Резерв на непредвиденные работы и материалы, 15 %				**195 183**						
	ВСЕГО ориентировочно (без оборудования и позиций по КП)				**1 496 405**						

Примечания

1. Смета ориентировочная, не коммерческое предложение: объёмы — из ведомости объёмов работ и спецификации материалов, цены — нижняя граница открытых прайсов Москвы (прайсы собраны 21.09.2026, часть расценок сверена повторно 08.11.2026); перед договором цены подтвердить у подрядчика и поставщиков.
2. Источники цен: Ц1 — Домашний мастерок: прайс на отделочные работы, 2026; Ц2 — Домашний мастерок: прайс на плиточные работы, 2026; Ц3 Домашний мастерок: прайс на электромонтажные работы, 2026; Ц4 — Профи ремонтник: штукатурно-малярные работы; Ц5 — Profi.ru: укладка керамогранита на стены, Москва 2026; Ц6 — knowledge/spec-materials.md, разд. 1 и 3: ориентир по сегментам; Ц7 — Розница Москвы, 09.2026: Лемана ПРО, KGSnab, официальный дилер Farrow & Ball.
3. Повторная сверка с прайсом: 08.11.2026 — гофра слаботочки с затяжкой; остальные расценки — по прайсам, собранным 21.09.2026.
4. В итог не вошли позиции «по КП» и «по факту»: оборудование и мебель, двери, материалы с расходом по ТУ, вывоз мусора, подъём и уборка.
5. Доставка — 10 % от материалов, резерв — 15 % (частный ремонт 10–20 %) отдельными строками, в количествах не спрятаны. Графы «факт» и «разница» заполняются по актам.

Допущения и предложения на листе

Основа листа: размеры сняты с плана заказчика, контрольный обмер не выполнен (К-5); высота потолка 2700 мм принята: на плане заказчика не указана (К-5); подрайон климата не задан — принят не северный (жилые от 2,5 м) (К-4); толщины стен приняты: наружные 250 мм, перегородки 120 мм — не обмерены (К-5); разрешённая мощность 15 кВт принята по типовой квартире, технических условий нет (К-6).

См. лист открытых вопросов (лист 6, записи К-4–К-6).

Изм.	Кол.уч	Лист	№ док.	Подп.	Дата
Разраб.		Кырлан А.С.			14.11.26
Пров.					
ГИП					
Н. контр.					
Утв.					

ГД-2026-006-АИ

Квартира 58 м²

Общая площадь 55,23* м² · * размеры приняты, не замерены (реестр — л. 6, 7, К-5)

Дизайн-проект интерьера

Стадия	Лист	Листов
РП	101	108

Смета ориентировочная (окончание)

М б/м

Кырлан Александр Сергеевич

Смета проекта: этапы, помещения, итог

Весь проект: ремонт, мебель, свет, техника, декор · вилка «от … до …» · позиции «по КП» посчитаны отдельно · цены — ориентир, не оферта

Смета проекта: весь проект по категориям (прайсы собраны 21.09.2026, часть расценок сверена повторно 08.11.2026)

Категория	Позиций	С ценой	По КП	Сумма по позициям с ценой, ₽
Ремонт: работы	51	32	19	656 514
Ремонт: материалы отделки и черновые	27	12	15	586 098
Электрика: кабель, механизмы, щит	31	0	31	
Сантехника: приборы, трубы, арматура	34	0	34	
Доставка и услуги	4	1	3	58 610
Мебель (включая кухню)	14	0	14	
Свет: светильники и ленты	17	0	17	
Техника	4	0	4	
Декор и текстиль	35	0	35	
ИТОГО по позициям с ценой (цены — нижняя граница открытых прайсов)	**217**	**45**	**172**	**1 301 222**
Резерв на непредвиденные работы и материалы, 15 % от ремонта				195 183
ВЕСЬ ПРОЕКТ — вилка «от … до …», ₽				**1 301 222 … 1 496 405**
Позиции «по КП» — цена не названа, в итог НЕ входят: работы — 19; материалы отделки и черновые — 15; электрика: кабель, механизмы, щит — 31; сантехника: приборы, трубы, арматура — 34; доставка и услуги — 3; мебель (включая кухню) — 14; свет: светильники и ленты — 17; техника — 4; декор и текстиль — 35			**172**	**итог выше на их цену**

По этапам

Этап	Поз.	С ценой	Сумма, ₽
Демонтаж и черновые работы (работы)	10	5	121 170
Инженерные системы (работы)	23	11	76 266
Чистовые работы (работы)	18	16	459 078
Черновые материалы (смеси, ГКЛ, гидроизоляция)	13	2	23 400
Электрика: кабель, механизмы, щит, слаботочка	31	0	
Сантехника: приборы, трубы, арматура	34	0	
Чистовые материалы (отделка, двери)	14	10	562 698
Доставка и услуги	4	1	58 610
Резерв на непредвиденное, 15 %	1	1	195 183
Итого ремонт (с резервом)			**1 496 405**

По помещениям

Помещение	Работы, ₽	Материалы, ₽	Всего, ₽
Общее по объекту (без привязки к помещению)	8 262		8 262
1. Кухня-гостиная	186 799	130 068	316 867
2. Спальня	129 064	89 125	218 189
3. Ванная	78 198	160 593	238 791
4. Санузел	63 083	134 356	197 439
5. Прихожая	116 424	27 418	143 842
6. Гардеробная	74 684	44 538	119 222
Доставка и услуги			58 610
Резерв 15 %			195 183
Итого ремонт (с резервом)			**1 496 405**

Работы по этапам с расценками (ориентир)

№	Работа	Ед.	Объём	Расценка, ₽	Сумма, ₽	Расценка	Чей подряд
1. Демонтаж и черновые работы — работы, ориентир по открытым прайсам							
1	Демонтаж существующего покрытия пола до основания	м²	55,23	по КП			бригада
2	Демонтаж существующей отделки стен до основания	м²	153,55	по КП			бригада

Допущения и предложения на листе

Основа листа: размеры сняты с плана заказчика, контрольный обмер не выполнен (К-5); высота потолка 2700 мм принята: на плане заказчика не указана (К-5); подрайон климата не задан — принят не северный (жилые от 2,5 м) (К-4); толщины стен приняты: наружные 250 мм, перегородки 120 мм — не обмерены (К-5); разрешённая мощность 15 кВт принята по типовой квартире, технических условий нет (К-6).

См. лист открытых вопросов (лист 6, записи К-4–К-6).

Изм.	Кол.уч	Лист	№ док.	Подп.	Дата
Разраб.		Кырлан А.С.			14.11.26
Пров.					
ГИП					
Н. контр.					
Утв.					

ГД-2026-006-АИ

Квартира 58 м²

Общая площадь 55,23* м² · * размеры приняты, не замерены (реестр — л. 6, 7, К-5)

Дизайн-проект интерьера

Стадия	Лист	Листов
РП	102	108

Смета проекта: этапы, помещения, итог

М б/м

Кырлан Александр Сергеевич

Смета проекта: этапы, помещения, итог (продолжение)

ПРЕДВАРИТЕЛЬНО · не для производства работ · открыто пунктов: 9 (реестр — л. 6, 7)

Весь проект: ремонт, мебель, свет, техника, декор · вилка «от … до …» · позиции «по КП» посчитаны отдельно · цены — ориентир, не оферта

Работы по этапам с расценками (ориентир) (продолжение)

№	Работа	Ед.	Объём	Расценка, ₽	Сумма, ₽	Расценка	Чей подряд
3	Демонтаж существующей отделки потолка до основания	м²	55,23	по КП			бригада
4	Демонтаж существующих дверных блоков	шт	6,00	по КП			бригада
5	Демонтаж существующих сантехприборов и электрооборудования (если есть)	компл		по КП			бригада
6	Устройство стяжки: стяжка ЦПС М200, 50 мм	м²	55,81	530	29 579	Ц1	бригада
7	Гидроизоляция обмазочная, 2 слоя: пол, стены на 200 мм, зоны замачивания	м²	7,07	450	3 182	Ц1	бригада
8	Штукатурка стен по маякам, до 10 мм	м²	24,67	530	13 075	Ц1	бригада
9	Штукатурка оконных откосов шириной до 200 мм	м²	2,59	540	1 399	Ц4	бригада
10	Потолок ГКЛ по каркасу П113, 1 слой	м²	49,29	1 500	73 935	Ц1	бригада
2. Инженерные системы — работы, ориентир по открытым прайсам							
11	Прокладка слаботочной линии: Кабель домофона — тип по системе поставщика, отдельно от силовых	м	3,40	по КП			бригада
12	Прокладка слаботочной линии: Кабель коаксиальный RG-6 (75 Ом) к розеткам ТВ, отдельно от силовых	м	16,30	по КП			бригада
13	Прокладка слаботочной линии: Кабель U/UTP кат. 5e (LAN, Wi-Fi и камеры по PoE), отдельно от силовых	м	30,10	по КП			бригада
14	Прокладка гофротрубы Ø20 для слаботочных линий, отдельно от силовых	м	44,80	140	6 272	Ц3	бригада
15	Сборка слаботочного щита ЩС**: корпус, патч-панель, подключение линий и питания 220 В; коммутатор и точки доступа — оборудование заказчика	шт	1,00	по КП			бригада
16	Электроточка: подрозетник в бетоне, розетка, выключатель, вывод	шт	33,00	950	31 350	Ц3	бригада
17	Штробы в стенах под спуски кабеля к точкам — выполняются только после технического заключения о несущих стенах	м	59,00	по КП			бригада
18	Установка встраиваемого точечного светильника	шт	4,00	750	3 000	Ц3	бригада
19	Монтаж светильника: потолочного, подвесного, настенного	шт	8,00	1 200	9 600	Ц3	бригада
20	Монтаж LED-ленты в алюминиевый профиль	м	1,80	230	414	Ц3	бригада
21	Установка блока питания LED в доступном месте (люк, шкаф)	шт	2,00	570	1 140	Ц3	бригада
22	Установка автономного пожарного извещателя	шт	3,00	по КП			бригада
23	Сборка щита: установка автоматов и АВДТ групп, вводного автомата	шт	7,00	230	1 610	Ц3	бригада
24	Установка вводного УЗО	шт	1,00	380	380	Ц3	бригада
25	Монтаж инсталляции, установка подвесного унитаза и кнопки смыва	шт	1,00	10 500	10 500	Ц1	бригада
26	Короб инсталляции: каркас и обшивка ГКЛВ в 2 слоя, ревизионный доступ к смыву	шт	1,00	по КП			бригада
27	Короб стояков Ш1 489 × 319 мм (внутренний 436 × 266): каркас и обшивка ГКЛВ в 2 слоя, ревизионный люк 300 × 400	м²	2,11	по КП			бригада
28	Короб К1 над чистым полом: каркас и обшивка ГКЛВ под плитку (материалы — в спецификации ВК)	м	1,46	по КП			бригада
29	Установка ванны с сифоном	шт	1,00	6 000	6 000	Ц1	бригада
30	Установка умывальника (мойки) с сифоном и смесителем	шт	2,00	3 000	6 000	Ц1	бригада
31	Подключение стиральной (посудомоечной) машины к ВК	шт	1,00	по КП			бригада
32	Установка радиатора с узлом подключения и терморегулятором	шт	3,00	по КП			бригада
33	Монтаж сплит-системы КВ-1**: внутренний блок на стене, трасса фреона и дренажа до наружного блока, вакуумирование, пусконаладка; наружный блок в корзине на фасаде (высотные работы)	шт	2,00	по КП			бригада

Допущения и предложения на листе

Основа листа: размеры сняты с плана заказчика, контрольный обмер не выполнен (К-5); высота потолка 2700 мм принята: на плане заказчика не указана (К-5); подрайон климата не задан — принят не северный (жилые от 2,5 м) (К-4); толщины стен приняты: наружные 250 мм, перегородки 120 мм — не обмерены (К-5); разрешённая мощность 15 кВт принята по типовой квартире, технических условий нет (К-6).

Знак «**» — предложение проектировщика, заказчиком не утверждено (согласовать с заказчиком): ЩС — щит слаботочный: место и состав; ИЗ-3: КВ-1 — длина петли принята по типовому минимуму 3 м; паспорта выбранной модели нет Внутренний блок перенесён со стены А (offset 3300…4200 — внутри оконного проёма 3200…4800) на стену Г, offset 300…1200 (простенок у окна 1, поток вдоль помещения к дивану); наружный блок КН-1 — в простенок между окнами (стена А, 2400…3200).

См. лист открытых вопросов (лист 6, записи К-4–К-6; лист 7, запись ИЗ-3).

Изм.	Кол.уч	Лист	№ док.	Подп.	Дата
Разраб.		Кырлан А.С.			14.11.26
Пров.					
ГИП					
Н. контр.					
Утв.					

ГД-2026-006-АИ

Квартира 58 м²

Общая площадь 55,23* м² · * размеры приняты, не замерены (реестр — л. 6, 7, К-5)

Дизайн-проект интерьера

Стадия	Лист	Листов
РП	103	108

Смета проекта: этапы, помещения, итог (продолжение)

М б/м

Кырлан Александр Сергеевич

Смета проекта: этапы, помещения, итог (окончание)

ПРЕДВАРИТЕЛЬНО · не для производства работ · открыто пунктов: 9 (реестр — л. 6, 7)

Весь проект: ремонт, мебель, свет, техника, декор · вилка «от … до …» · позиции «по КП» посчитаны отдельно · цены — ориентир, не оферта

Работы по этапам с расценками (ориентир) (продолжение)

№	Работа	Ед.	Объём	Расценка, ₽	Сумма, ₽	Расценка	Чей подряд
3. Чистовые работы — работы, ориентир по открытым прайсам							
34	Облицовка стен керамогранитом 1200×600 на клею	м²	28,35	2 500	70 875	Ц5	бригада
35	Облицовка короба инсталляции (ГКЛВ) керамогранитом: лицо, боковины, полка	м²	3,46	2 500	8 650	Ц5	бригада
36	Укладка керамогранита на пол, 600×600, на клею	м²	14,73	1 800	26 514	Ц2	бригада
37	Затирка швов керамогранита	м²	46,11	150	6 917	Ц2	бригада
38	Грунтование стен, 2 слоя (под штукатурку и под отделку)	м²	153,55	96	14 741	Ц4	бригада
39	Шпаклёвка стен под окраску, 2 слоя (старт и финиш), уровень Q3	м²	122,49	750	91 868	Ц1	бригада
40	Грунтование и шпаклёвка оконных откосов, 2 слоя	м	14,40	300	4 320	Ц4	бригада
41	Грунтование потолка, 2 слоя	м²	55,23	96	5 302	Ц4	бригада
42	Шпаклёвка потолка под окраску, 2 слоя, уровень Q3	м²	55,23	950	52 469	Ц1	бригада
43	Окраска потолка водно-дисперсионной краской, 2 слоя	м²	55,23	360	19 883	Ц1	бригада
44	Окраска стен водно-дисперсионной краской, 2 слоя	м²	145,50	300	43 650	Ц1	бригада
45	Окраска оконных откосов, 2 слоя	м	14,40	120	1 728	Ц4	бригада
46	Укладка инженерной доски на клей	м²	41,08	1 200	49 296	Ц1	бригада
47	Установка плинтуса МДФ h=110 мм	м	48,82	450	21 969	Ц1	бригада
48	Окраска плинтуса в тоне S 0300-N, 2 слоя	м	48,82	300	14 646	Ц1	бригада
49	Монтаж дверей скрытого монтажа под покраску (поставщик дверей)	шт	5,00	5 250	26 250	Ц1	поставщик
50	Входная дверь, поставка с монтажом и откосами	шт	1,00	по КП			поставщик
51	Монтаж телевизора M20 на кронштейн, скрытая прокладка HDMI и питания (штроба, трубка), подключение акустики	шт	1,00	по КП			бригада
4. Прочие работы и услуги — работы, ориентир по открытым прайсам							
52	Кухонный гарнитур по проекту кухни, изготовление и монтаж (4–8 нед.)	компл	1,00	по КП			поставщик
	Итого работы (позиции с расценкой)				**656 514**		

Примечания

1. Итог «ВЕСЬ ПРОЕКТ» — не прогноз, а сумма того, у чего есть цена: ремонт (работы и материалы по смете сметчика), мебель, свет, техника и декор — по ценам из данных проекта. Позиции без цены названы «по КП» (172 шт.) и в итог не входят: пока цена не названа, итог выше напечатанного.
2. Вилка: «от» — сумма по позициям с ценой по нижней границе открытых прайсов (прайсы собраны 21.09.2026, часть расценок сверена повторно 08.11.2026, Москва); «до» — «от» плюс резерв на непредвиденное (15 % от ремонта; частный ремонт 10–20 %).
3. Работы — ориентир по прайсам подрядчиков, не договорная цена: расценку называет бригада после контрольного обмера. Материалы — по «Смете материалов с ценами» (следующий лист).
4. Разбивка по помещениям — доли: общая закупка делится пропорционально площади (длине, числу), по которой считается позиция; работы — по объёму строки в помещении. Сумма по помещениям, по этапам и по категориям одна и та же.
5. Источники расценок и цен: Ц1 — Домашний мастерок: прайс на отделочные работы, 2026; Ц2 — Домашний мастерок: прайс на плиточные работы, 2026; Ц3 — Домашний мастерок: прайс на электромонтажные работы, 2026; Ц4 — Профи ремонтник: штукатурно-малярные работы; Ц5 — Profi.ru: укладка керамогранита на стены, Москва 2026; Ц6 — справочник материалов: ориентир по сегментам; Ц7 — Розница Москвы, 09.2026: Лемана ПРО, KGSnab, официальный дилер Farrow & Ball.
6. Оборудование «по КП» из сметы сметчика (кухня и др.): 1 поз. — в позиции «по КП» мебели и техники.

Допущения и предложения на листе

Основа листа: размеры сняты с плана заказчика, контрольный обмер не выполнен (К-5); высота потолка 2700 мм принята: на плане заказчика не указана (К-5); подрайон климата не задан — принят не северный (жилые от 2,5 м) (К-4); толщины стен приняты: наружные 250 мм, перегородки 120 мм — не обмерены (К-5); разрешённая мощность 15 кВт принята по типовой квартире, технических условий нет (К-6).

См. лист открытых вопросов (лист 6, записи К-4–К-6).

Изм.	Кол.уч	Лист	№ док.	Подп.	Дата
Разраб.		Кырлан А.С.			14.11.26
Пров.					
ГИП					
Н. контр.					
Утв.					

ГД-2026-006-АИ

Квартира 58 м²

Общая площадь 55,23* м² · * размеры приняты, не замерены (реестр — л. 6, 7, К-5)

Дизайн-проект интерьера

Стадия	Лист	Листов
РП	104	108

Смета проекта: этапы, помещения, итог (окончание)

М б/м

Кырлан Александр Сергеевич

Смета материалов с ценами

ПРЕДВАРИТЕЛЬНО · не для производства работ · открыто пунктов: 9 (реестр — л. 6, 7)

Все материалы с количеством, запасом, упаковкой, ценой и сроком · цены — ориентир по открытым прайсам, не оферта · работы не входят

Смета материалов с ценами

№	Позиция	Ед.	Нетто	Запас	С запасом	К закупке (упаковка)	Цена за ед., ₽	Сумма, ₽	Заказать заранее	Доп.
Чистовая отделка — позиций 14, с ценой 10, итого 562 698 ₽										
Покрытия полов и облицовка										
1	Инженерная доска (дуб натуральный, рабочий слой 4 мм, эмиссия E1, прямая укладка)	м²	41,08	7 %	43,96	44,00 м²	4 513 / м²	198 572		1, 8
2	Керамогранит 600×600 мм SG651622R	шт	48	13 %	54	54 шт · коробка	1 800 / м²	34 992		8
3	Керамогранит 1200×600 мм 610015000370	шт	87	13 %	98	98 шт · коробка	3 500 / м²	246 960		8
Лакокрасочные материалы										
4	Краска интерьерная акриловая, полуматовая, класс истирания 1 — Tikkurila S 1002-Y50R	л	9,90	10 %	10,89	5 банка · банка 2,7 л	3 510 / банк	17 550		8
5	Краска интерьерная водно-дисперсионная, глубокоматовая, класс истирания 1 — Tikkurila S 0300-N	л	11,83	10 %	13,01	5 банка · банка 2,7 л	3 510 / банк	17 550		8
6	Краска интерьерная акриловая, глубокоматовая, класс истирания 2 — Tikkurila S 1502-Y50R	л	8,14	10 %	8,95	4 банка · банка 2,7 л	3 510 / банк	14 040		8
7	Краска интерьерная акриловая, полуматовая, класс истирания 1 — Tikkurila S 1502-Y50R	л	5,44	10 %	5,98	3 банка · банка 2,7 л	3 510 / банк	10 530		8
8	Краска интерьерная акриловая, матовая, класс истирания 1 — Tikkurila Harmony V503 «Winter»	л	5,92	10 %	6,51	3 банка · банка 2,7 л	3 510 / банк	10 530		8
9	Краска интерьерная акриловая, глубокоматовая, класс истирания 2 — Tikkurila Anti-Reflex 2 V503 «Winter»	л	1,43	10 %	1,57	1 банка · банка 2,7 л	3 510 / банк	3 510		8
Погонажные изделия и потолки										
10	Плинтус напольный МДФ под покраску, h=110 мм, крепление к стене — SX184	м	48,82	10 %	53,70	23 шт · хлыст 2,4 м	368 / шт	8 464		8
Двери										
11	Дверь входная Д-1, проём 900×2100 мм	шт	1		1	1 шт	по запросу			6
12	Дверь скрытого монтажа (короб под покраску) Д-2, проём 900×2100 мм, Софья (SOFIA) Скрытые двери Модель 07	шт	1		1	1 шт	по запросу		≈ 30 дн.	6, 7
13	Дверь скрытого монтажа (короб под покраску) Д-3, проём 800×2100 мм, Софья (SOFIA) Скрытые двери Модель 07	шт	2		2	2 шт	по запросу		≈ 30 дн.	6, 7
14	Дверь скрытого монтажа (короб под покраску) Д-4, проём 700×2100 мм, Софья (SOFIA) Скрытые двери Модель 07	шт	2		2	2 шт	по запросу		≈ 30 дн.	6, 7
Черновые материалы — позиций 13, с ценой 2, итого 23 400 ₽										
Покрытия полов и облицовка										
15	Клей для паркетной и инженерной доски (эластичный, по ТУ изготовителя доски)	м²	41,08		41,08	фасовка по ТУ изделия	по запросу			2
Сухие смеси и гидроизоляция										
16	Клей плиточный цементный класса C2 S1 (ГОСТ Р 56387-2018)	кг	24,94	10 %	27,43	2 мешок · мешок 25 кг	1 800 / меш.	3 600		8
17	Клей плиточный цементный класса C2 (ГОСТ Р 56387-2018)	кг	240,94	10 %	265,03	11 мешок · мешок 25 кг	1 800 / меш.	19 800		8
18	Затирка цементная класса класс не задан, цвет — по колерной карте	кг	3,51	10 %	3,86	2 упаковка · упак. 2 кг	по запросу			
19	Гидроизоляция обмазочная полимерная, 2 слоя, лента в углах, манжеты на выводах	м²	7,07	10 %	7,78	фасовка по ТУ изделия	по запросу			2
20	Лента демпферная по периметру пола из плитки	м	19,14	10 %	21,05	22,00 м	по запросу			
21	Смесь цементно-песчаная для стяжки М200 (50 мм, 33 мм)	м³	2,71	5 %	2,85	фасовка по ТУ изделия	по запросу			2
22	Смесь штукатурная гипсовая для машинного и ручного нанесения по маякам, слой до 10 мм	м²	24,67	10 %	27,14	фасовка по ТУ изделия	по запросу			2
Короба из ГКЛВ										

Допущения и предложения на листе

Основа листа: размеры сняты с плана заказчика, контрольный обмер не выполнен (К-5); высота потолка 2700 мм принята: на плане заказчика не указана (К-5); подрайон климата не задан — принят не северный (жилые от 2,5 м) (К-4); толщины стен приняты: наружные 250 мм, перегородки 120 мм — не обмерены (К-5); разрешённая мощность 15 кВт принята по типовой квартире, технических условий нет (К-6).

Знак «**» — предложение проектировщика, заказчиком не утверждено (согласовать с заказчиком): пол пом. 1, 2, 6 — артикул изделия не выбран: позиция описана характеристиками («аналог по характеристикам»), артикул выбирается при закупке.

См. лист открытых вопросов (лист 6, записи К-4–К-6).

Изм.	Кол.уч	Лист	№ док.	Подп.	Дата
Разраб.		Кырлан А.С.			14.11.26
Пров.					
ГИП					
Н. контр.					
Утв.					

ГД-2026-006-АИ

Квартира 58 м²

Общая площадь 55,23* м² · * размеры приняты, не замерены (реестр — л. 6, 7, К-5)

Дизайн-проект интерьера

Стадия	Лист	Листов
РП	105	108

Смета материалов с ценами

М б/м

Кырлан Александр Сергеевич

Смета материалов с ценами (продолжение)

Все материалы с количеством, запасом, упаковкой, ценой и сроком · цены — ориентир по открытым прайсам, не оферта · работы не входят

Смета материалов с ценами (продолжение)

№	Позиция	Ед.	Нетто	Запас	С запасом	К закупке (упаковка)	Цена за ед., ₽	Сумма, ₽	Заказать заранее	Доп.
23	Лист ГКЛВ 12,5 мм, 2500 × 1200 мм, обшивка коробов в 2 слоя	м²	4,22	10 %	4,64	2 лист · лист 3,00 м²	по запросу			
24	Профиль стальной оцинкованный 27 × 28 мм: каркас коробов (стойки и направляющие)	м	12,08	10 %	13,29	5 шт · хлыст 3 м	по запросу			
Лакокрасочные материалы										
25	Шпаклёвка финишная полимерная под окраску (стены и потолки, Q3)	м²	177,72	10 %	195,49	фасовка по ТУ изделия	по запросу			2
26	Грунтовка акриловая глубокого проникновения, 2 слоя	м²	208,78	10 %	229,66	фасовка по ТУ изделия	по запросу			2
Погонажные изделия и потолки										
27	Потолок подвесной ГКЛ/ГКЛВ по каркасу Knauf П113: листы, профили, подвесы, лента, шпаклёвка швов	м²	49,29		49,29	фасовка по ТУ изделия	по запросу			2
Электрика и слаботочные сети — позиций 31, с ценой 0, итого 0 ₽										
Слаботочные сети										
28	Кабель домофона — тип по системе поставщика	м	3,40		3,40	4,00 м	по запросу			3
29	Кабель коаксиальный RG-6 (75 Ом) к розеткам ТВ	м	16,30		16,30	17,00 м	по запросу			3
30	Кабель U/UTP кат. 5e (LAN, Wi-Fi и камеры по PoE)	м	30,10		30,10	31,00 м	по запросу			3
31	Гофротруба Ø20 для слаботочных линий, отдельно от силовых	м	44,80		44,80	45,00 м	по запросу			3
32	Розетка компьютерная RJ45, кат. 6, с рамкой и подрозетником	шт	2		2	2 шт	по запросу			
33	Розетка телевизионная (коаксиальная) с рамкой и подрозетником	шт	1		1	1 шт	по запросу			
34	Трубка или монитор домофона (поставка домофонной организации)	шт	1		1	1 шт	по запросу			
35	Щит слаботочный ЩС**: корпус, DIN-рейка, розетки 220 В	шт	1		1	1 шт	по запросу			
36	Патч-панель, портов не менее 2	шт	1		1	1 шт	по запросу			
Электрика: щит										
37	Автоматический выключатель C10 A, 1P	шт	1		1	1 шт	по запросу			4
38	Автоматический выключатель C16 A, 1P	шт	4		4	4 шт	по запросу			4
39	Автоматический выключатель C32 A, 1P	шт	1		1	1 шт	по запросу			4
40	Корпус щита ЩРВ-П-24, IP41, 24 модулей	шт	1		1	1 шт	по запросу			4
41	Вводной автомат C63, 2P	шт	1		1	1 шт	по запросу			4
42	Вводное УЗО-S 63 A, 100 мА (селективное)	шт	1		1	1 шт	по запросу			4
43	УЗИП тип 2	шт	1		1	1 шт	по запросу			4
Электрика: механизмы и изделия										
44	Розетка с з/к и защитными шторками, 16 А	шт	17		17	17 шт	по запросу			4
45	Розетка IP44 с крышкой, 16 А	шт	2		2	2 шт	по запросу			4
46	Выключатель 1-клав.	шт	5		5	5 шт	по запросу			4
47	Выключатель 1-клав. проходной	шт	2		2	2 шт	по запросу			4

Допущения и предложения на листе

Основа листа: размеры сняты с плана заказчика, контрольный обмер не выполнен (К-5); высота потолка 2700 мм принята: на плане заказчика не указана (К-5); подрайон климата не задан — принят не северный (жилые от 2,5 м) (К-4); толщины стен приняты: наружные 250 мм, перегородки 120 мм — не обмерены (К-5); разрешённая мощность 15 кВт принята по типовой квартире, технических условий нет (К-6).

Знак «**» — предложение проектировщика, заказчиком не утверждено (согласовать с заказчиком): ЩС — щит слаботочный: место и состав; пол пом. 1, 2, 6 — артикул изделия не выбран: позиция описана характеристиками («аналог по характеристикам»), артикул выбирается при закупке.

См. лист открытых вопросов (лист 6, записи К-4–К-6).

Изм.	Кол.уч	Лист	№ док.	Подп.	Дата
Разраб.		Кырлан А.С.			14.11.26
Пров.					
ГИП					
Н. контр.					
Утв.					

ГД-2026-006-АИ

Квартира 58 м²

Общая площадь 55,23* м² · * размеры приняты, не замерены (реестр — л. 6, 7, К-5)

Дизайн-проект интерьера

Стадия	Лист	Листов
РП	106	108

Смета материалов с ценами (продолжение)

М б/м

Кырлан Александр Сергеевич

Смета материалов с ценами (продолжение)

Все материалы с количеством, запасом, упаковкой, ценой и сроком · цены — ориентир по открытым прайсам, не оферта · работы не входят

Смета материалов с ценами (продолжение)

№	Позиция	Ед.	Нетто	Запас	С запасом	К закупке (упаковка)	Цена за ед., ₽	Сумма, ₽	Заказать заранее	Доп.
48	Выключатель 2-клав. проходной	шт	2		2	2 шт	по запросу			4
49	Рамка 1-постовая	шт	24		24	24 шт	по запросу			4
50	Рамка 2-постовая	шт	2		2	2 шт	по запросу			4
51	Коробка установочная (подрозетник) Ø68	шт	28		28	28 шт	по запросу			4
52	Вывод кабеля под прибор (клеммник)	шт	3		3	3 шт	по запросу			4
53	Вывод кабеля к вентилятору вытяжки	шт	1		1	1 шт	по запросу			4
54	Коробка уравнивания потенциалов КУП	шт	1		1	1 шт	по запросу			4
55	Блок питания LED 24 В, 100 Вт	шт	1		1	1 шт	по запросу			4
56	Блок питания LED 24 В, 60 Вт	шт	1		1	1 шт	по запросу			4
57	Извещатель дымовой автономный	шт	2		2	2 шт	по запросу			4
58	Извещатель тепловой	шт	1		1	1 шт	по запросу			4
Сантехника — позиций 34, с ценой 0, итого 0 ₽										
Сантехника: санитарные приборы										
59	Ванна встраиваемая акриловая 1500×700 мм, с каркасом, экраном и отверстием слив-перелив — акриловая 1500×700, смеситель настенный	шт	1		1	1 шт	по запросу			5
60	Унитаз подвесной безободковый, с сиденьем микролифт, крепёж и звукоизолирующая прокладка — Laufen Pro 8.2096.6.000.000.1	шт	1		1	1 шт	по запросу			5
61	Инсталляция для подвесного унитаза: рама высотой 1120 мм, бачок, клавиша смыва (ось клавиши 1050 мм от чистого пола)	шт	1		1	1 шт	по запросу			5, 1
62	Умывальник подвесной 450×450 мм, с отверстием под смеситель и переливом — Laufen Pro S 8.1096.3.000.104.1	шт	1		1	1 шт	по запросу			5
63	Мойка кухонная 700×480 мм, с переливом — мойка врезная 700×480 в шкафу М5	шт	1		1	1 шт	по запросу			5
64	Полотенцесушитель электрический, IP44, с терморегулятором	шт	1		1	1 шт	по запросу			5, 1
Сантехника: смесители, сифоны и арматура приборов										
65	Смеситель для ванны настенный однорычажный, межосевое 150 мм, с душевым набором (лейка, шланг, держатель)	шт	1		1	1 шт	по запросу			5, 1
66	Смеситель для умывальника однорычажный, с донным клапаном	шт	1		1	1 шт	по запросу			5, 1
67	Смеситель кухонный однорычажный, высокий излив	шт	1		1	1 шт	по запросу			5, 1
68	Обвязка ванны слив-перелив Ø40/50 с сифоном	шт	1		1	1 шт	по запросу			5, 1
69	Сифон для умывальника бутылочный Ø32/40–50, с гофрой к выпуску	шт	1		1	1 шт	по запросу			5, 1
70	Сифон для мойки Ø40/50	шт	1		1	1 шт	по запросу			5, 1
71	Сифон для стиральной машины встраиваемый в стену Ø50, с обратным клапаном	шт	1		1	1 шт	по запросу			5, 1
72	Кран угловой ½"×½" с гибкой подводкой 40 см (умывальники, мойка)	шт	4		4	4 шт	по запросу			5, 1
73	Кран шаровой угловой ½"×¾" для подключения стиральной и посудомоечной машины	шт	1		1	1 шт	по запросу			5, 1
Сантехника: трубопроводы										
74	Труба полипропиленовая PP-R PN20 Ø20×3,4 (В1) — ГОСТ 32415-2013	м	13,50	10 %	13,50	13,50 м	по запросу			5

Допущения и предложения на листе

Основа листа: размеры сняты с плана заказчика, контрольный обмер не выполнен (К-5); высота потолка 2700 мм принята: на плане заказчика не указана (К-5); подрайон климата не задан — принят не северный (жилые от 2,5 м) (К-4); толщины стен приняты: наружные 250 мм, перегородки 120 мм — не обмерены (К-5); разрешённая мощность 15 кВт принята по типовой квартире, технических условий нет (К-6).

Знак «**» — предложение проектировщика, заказчиком не утверждено (согласовать с заказчиком): пол пом. 1, 2, 6 — артикул изделия не выбран: позиция описана характеристиками («аналог по характеристикам»), артикул выбирается при закупке.

См. лист открытых вопросов (лист 6, записи К-4–К-6).

Изм.	Кол.уч	Лист	№ док.	Подп.	Дата
Разраб.		Кырлан А.С.			14.11.26
Пров.					
ГИП					
Н. контр.					
Утв.					

ГД-2026-006-АИ

Квартира 58 м²

Общая площадь 55,23* м² · * размеры приняты, не замерены (реестр — л. 6, 7, К-5)

Дизайн-проект интерьера

Стадия	Лист	Листов
РП	107	108

Смета материалов с ценами (продолжение)

М б/м

Кырлан Александр Сергеевич

Смета материалов с ценами (окончание)

Все материалы с количеством, запасом, упаковкой, ценой и сроком · цены — ориентир по открытым прайсам, не оферта · работы не входят

Смета материалов с ценами (продолжение)

№	Позиция	Ед.	Нетто	Запас	С запасом	К закупке (упаковка)	Цена за ед., ₽	Сумма, ₽	Заказать заранее	Доп.
75	Труба PP-R, армированная стекловолокном, PN20 Ø20×2,8 (Т3**) — ГОСТ 32415-2013	м	9,50	10 %	9,50	9,50 м	по запросу			5
76	Труба канализационная ПП Ø40 (К1) — ГОСТ 32414-2013	м	2,50	10 %	2,50	2,50 м	по запросу			5
77	Труба канализационная ПП Ø50 (К1) — ГОСТ 32414-2013	м	8,00	10 %	8,00	8,00 м	по запросу			5
78	Труба канализационная ПП Ø110 (К1) — ГОСТ 32414-2013	м	1,50	10 %	1,50	1,50 м	по запросу			5
Сантехника: фасонные части и выводы										
79	Отвод канализационный ПП 45° Ø40 — ГОСТ 32414-2013	шт	2		2	2 шт	по запросу			5
80	Отвод канализационный ПП 45° Ø50 — ГОСТ 32414-2013	шт	12		12	12 шт	по запросу			5
81	Отвод канализационный ПП 45° Ø110 — ГОСТ 32414-2013	шт	6		6	6 шт	по запросу			5
82	Тройник канализационный ПП 45° (врезки ветвей) — ГОСТ 32414-2013	шт	4		4	4 шт	по запросу			5
83	Ревизия канализационная ПП (после поворота трассы) — ГОСТ 32414-2013	шт	5		5	5 шт	по запросу			5
84	Фитинги PP-R Ø20: тройники, угольники 90° (ветви и повороты В1, Т3**) — ГОСТ 32415-2013	шт	22		22	22 шт	по запросу			5
85	Водорозетка PP-R Ø20×½" настенная, с креплением — ГОСТ 32415-2013	шт	8		8	8 шт	по запросу			5
Сантехника: узлы ввода, люки, короба										
86	Кран шаровой латунный Ду15 PN16 (отключение ввода)	шт	2		2	2 шт	по запросу			5, 1
87	Фильтр сетчатый косой Ду15	шт	2		2	2 шт	по запросу			5, 1
88	Счётчик воды крыльчатый Ду15 (ХВ, ГВ), с поверкой	шт	2		2	2 шт	по запросу			5, 1
89	Клапан обратный Ду15	шт	2		2	2 шт	по запросу			5, 1
90	Люк ревизионный нажимной под плитку 300×400 мм	шт	1		1	1 шт	по запросу			5, 1
91	Звукоизоляция стояка К1 в коробе: рулонный звукоизоляционный материал ≥ 10 мм, обмотка стояка на высоту этажа	м	2,70		2,70	2,70 м	по запросу			5, 1
92	Короб К1 над полом: профиль ПН/ПС, ГКЛВ 12,5 мм под плитку	м	1,60		1,60	1,60 м	по запросу			5, 1
	ИТОГО материалы (позиций с ценой 12 из 92; без цены 80 — «по запросу», в итог не входят)							**586 098**		

Примечания

1. Количества — из единой книги материалов проекта: тот же расход, что в спецификации отделочных материалов, смете и списке покупок. Запас — на подрезку и бой; норма запаса печатается в графе «Запас», её основание — в отдельном документе «Смета на материалы».
2. Цены — нижняя граница открытых прайсов (прайсы собраны 21.09.2026, часть расценок сверена повторно 08.11.2026, Москва); не предложение (оферта) магазинов. Цены нет — «по запросу», позиция в итог не входит. Работы в эту смету не входят (они — на листе «Смета проекта»).
3. Доп. 1. Изделие не выбрано: позиция описана по характеристикам («аналог»); марка, артикул и цена определяются при выборе изделия.
4. Доп. 2. Фасовка не задана в данных: количество дано в мерах расчёта, число упаковок определяется по выбранному продукту (расход и тара — по ТУ).
5. Доп. 3. Длина кабеля — по длинам групп щита из данных электрика; запас на подрезку в длину не заложен — берите бухту с запасом 5–10 %.
6. Доп. 4. Механизмы, рамки и подрозетники — по ведомости изделий электрика; серию механизмов выбирает заказчик.
7. Доп. 5. Трубы и фасонные части — по трассам листа разводки, +10 % на подрезку (уже в количестве); модели приборов заказчик выбирает сам.
8. Доп. 6. Двери: цена и срок называет поставщик после выбора изделия; в смету стоят только если цена задана в данных.
9. Доп. 7. Срок поставки — из данных проекта; если срок не задан, указан типовой диапазон практики как ориентир, а не срок поставщика.
10. Доп. 8. Цена — нижняя граница открытых прайс-листов на дату сбора (книга цен проекта); не коммерческое предложение магазина.
11. Доп. 9. Доли по помещениям справочные: общая закупка делится пропорционально площади (длине, числу), по которой считается позиция.

Допущения и предложения на листе

Основа листа: размеры сняты с плана заказчика, контрольный обмер не выполнен (К-5); высота потолка 2700 мм принята: на плане заказчика не указана (К-5); подрайон климата не задан — принят не северный (жилые от 2,5 м) (К-4); толщины стен приняты: наружные 250 мм, перегородки 120 мм — не обмерены (К-5); разрешённая мощность 15 кВт принята по типовой квартире, технических условий нет (К-6).

Знак «**» — предложение проектировщика, заказчиком не утверждено (согласовать с заказчиком): пол пом. 1, 2, 6 — артикул изделия не выбран: позиция описана характеристиками («аналог по характеристикам»), артикул выбирается при закупке; ИЗ-4: Т3.

См. лист открытых вопросов (лист 6, записи К-4–К-6; лист 7, запись ИЗ-4).

Изм.	Кол.уч	Лист	№ док.	Подп.	Дата
Разраб.		Кырлан А.С.			14.11.26
Пров.					
ГИП					
Н. контр.					
Утв.					

ГД-2026-006-АИ

Квартира 58 м²

Общая площадь 55,23* м² · * размеры приняты, не замерены (реестр — л. 6, 7, К-5)

Дизайн-проект интерьера

Стадия	Лист	Листов
РП	108	108

Смета материалов с ценами (окончание)

М б/м

Кырлан Александр Сергеевич

11

Визуализации

Кырлан Александр Сергеевич

выпуск 14.11.2026 2 bcee049e32 · стр. 119 из 128



Ванная · стена Б

Квартира 58 м² · визуализация 1 из 9

выпуск 14.11.2026 № bcee049e32 · стр. 120 из 128



Ванная · стена B

Квартира 58 м² · визуализация 2 из 9

выпуск 14.11.2026 № bceе049e32 · стр. 121 из 128



Спальня · стена Б

Квартира 58 м² · визуализация 3 из 9

выпуск 14.11.2026 № bcee049e32 · стр. 122 из 128



Прихожая · общий вид

Квартира 58 м² · визуализация 4 из 9

выпуск 14.11.2026 № bcee049e32 · стр. 123 из 128



Кухня-гостиная · стена Б

Квартира 58 м² · визуализация 5 из 9

выпуск 14.11.2026 № bcee049e32 · стр. 124 из 128



Кухня-гостиная · стена B

Квартира 58 м² · визуализация 6 из 9



Кухня-гостиная · стена Г

Квартира 58 м² · визуализация 7 из 9

выпуск 14.11.2026 № bcee049e32 · стр. 126 из 128



Гардеробная · общий вид

Квартира 58 м² · визуализация 8 из 9



Санузел · общий вид

выпуск 14.11.2026 № bcee049e32 · стр. 128 из 128