L

LINEA

ДИЗАЙН-ПРОЕКТ ИНТЕРЬЕРА

Квартира 55 м²

кухня-гостиная и спальня



Визуализация кухни-гостиной · 3D

ОБЩАЯ ПЛОЩАДЬ	ПОМЕЩЕНИЙ	СТАДИЯ	ШИФР	ОСНОВА
55,23 м²	6, из них жилых 2	Проект · предварительно	ГД-2026-006-АИ	план заказчика, без обмера

Как оставить правку: кнопка «Правка к этому листу» в правом верхнем углу любого листа · все листы проекта: дизайн-студия-квартир.рф/review.html?p=gost-kv58

ПАЛИТРА ОТДЕЛКИ

NCS S 1502-Y50	NCS S 1002-Y50	V503	G503	NCS S 2002-Y
44 %	32 %	24 %	текстиль, декор	текстиль, декор

АВТОР ПРОЕКТА

Кырлан Александр Сергеевич

Ноябрь 2026

выпуск 14.11.2026 № 2b6bd7c078 · стр. 1 из 92

Объект

Квартира 58 м²: 57,6 м², помещений 6, из них жилых 2.

Стиль: скандинавский 100 %. Стадия: предварительный альбом без обмера, планировка по плану заказчика.

Открытых вопросов 7, конфликтов разделов 0; изменений утверждено 3, ждут подписи 2.

Розетки и выводы

19 розеток (рамок 17), 3 вывода кабеля под технику и свет, 6 групп щита — всё с высотами от чистого пола: листы 41, 44.

Что решено (подписано вами)

ИЗ-1 — ТВ1 (2400), LAN1 (2550) и розетка приставки (2400, H=300) — на стене Г по оси тумбы ОБ-01.

ИЗ-2 — Диван М-08 привязка 1000…3200 — перед проёмом 800 мм.

ИЗ-3 — КВ-1 — стена Г, привязка 300…1200 (простенок у окна 1), КН-1 — стена А, простенок между окнами 2400…3200.

Предложено, ждёт подписи: ИЗ-4, ИЗ-5

Что ждёт вашего ответа

вопросов 7; блокируют заказ или работы — 3, они первыми и выделены

№	Вопрос	Варианты · что будет без ответа	Нужен ответ
К-2	Ванная (пом. 3), 2140 × 1380 мм в чистоте, проём Д-4 у стены Б.	Решить: (а) принять расстановку; (б) душ с поддоном 900 × 900 у стены Г вместо ванны — перед приборами ≥ 750 мм, кадры ванной перерисовать; (в) другой вариант автора. Без ответа: ванна 1500 × 700 и умывальник у стены В…	**до заказа мебели и материалов**
К-3	Скрытые двери Д-2, Д-3, Д-4 стоят в существующих проёмах прихожей, размеров в свету нет: короб скрытой двери шире и выше полотна на 100–120 / 50–80 мм, полотно по проёму 2100…	Без ответа: блоки скрытых дверей не заказывать до замера; полотна на листах — расчётные («расч.»), проёмы не переносятся.	**до заказа дверных блоков**
К-5	Основа альбома — план заказчика без контрольного обмера: размеры помещений сняты с плана, высота потолка 2700 мм и толщины стен (наружные 250 мм, перегородки 120 мм) приняты —…	Без ответа: размеры, высота потолка и толщины стен — принятые; мебель на заказ, двери и каркас потолков не заказывать до обмера.	**до заказа мебели, дверей и каркаса потолков**
К-1	Вентканалы на плане заказчика не показаны: ВК-1 принят у перегородки ванной и санузла (со стороны прихожей), ВК-2 — у кухни.	Без ответа: решётки ванной и санузла — у ВК-1, кухни — у ВК-2; места — до обмера, лист перевыпустить по факту.	до потолков и коробов
К-4	Климатический подрайон (СП 131.13330) не задан: принят не северный — жилые комнаты и кухня под потолком от 2,5 м (СП 54, п. 5.12).	Без ответа: отметки потолков жилых — по 2,5 м; при северном подрайоне уровни ниже 2,7 м пересчитать до заказа каркаса.	до заказа каркаса потолков
К-6	Разрешённая мощность 15 кВт принята по типовой квартире, технических условий в материалах объекта нет.	Без ответа: вводной аппарат и группы щита — по 15 кВт; при меньшей мощности схему щита пересчитать до монтажа.	до утверждения однолинейной схемы щита
К-7	Места стиральной машины в квартире не было.	Без ответа: стиральная машина ОБ-02 в кухне под столешницей (ниша вместо М-05, 2800…3420) — как на листах.	до заказа кухни

Полный текст каждого вопроса, варианты и рекомендация — на листах 71, 72 реестра открытых вопросов.

	Лист	№ док.	Подпись	Дата	Проект: Квартира 58 м²			
Дизайнер	Кырлан А.С.			14.11.26	Ваш проект на одной странице	Стадия	Лист	Листов
Проверил						П	2	92
Н. контр.								
Утв.								



	Лист	№ док.	Подпись	Дата	Проект: Квартира 58 м²			
Дизайнер	Кырлан А.С.			14.11.26	Визуализация кухни-гостиной	Стадия	Лист	Листов
Проверил						П	3	92
Н. контр.								
Утв.								



	Лист	№ док.	Подпись	Дата	Проект: Квартира 58 м²			
Дизайнер	Кырлан А.С.			14.11.26				
Проверил					Визуализация кухни-гостиной	Стадия	Лист	Листов
Н. контр.						П	4	92
Утв.								

выпуск 14.11.2026 № 2b6bd7c078 · стр. 4 из 92



	Лист	№ док.	Подпись	Дата	Проект: Квартира 58 м²			
Дизайнер	Кырлан А.С.			14.11.26				
Проверил					Визуализация кухни-гостиной	Стадия	Лист	Листов
Н. контр.								
Утв.						П	5	92

выпуск 14.11.2026 № 2b6bd7c078 · стр. 5 из 92



	Лист	№ док.	Подпись	Дата
Дизайнер	Кырлан А.С.			14.11.26
Проверил				
Н. контр.				
Утв.				

Проект: Квартира 58 м²

Визуализация спальни	Стадия	Лист	Листов
	П	6	92

выпуск 14.11.2026 № 2b6bd7c078 · стр. 6 из 92



	Лист	№ док.	Подпись	Дата	Проект: Квартира 58 м²			
Дизайнер	Кырлан А.С.			14.11.26				
Проверил					Визуализация ванной	Стадия	Лист	Листов
Н. контр.						П	7	92
Утв.								



	Лист	№ док.	Подпись	Дата	Проект: Квартира 58 м²			
Дизайнер	Кырлан А.С.			14.11.26				
Проверил					Визуализация ванной	Стадия	Лист	Листов
Н. контр.								
Утв.						П	8	92

выпуск 14.11.2026 № 2b6bd7c078 · стр. 8 из 92



	Лист	№ док.	Подпись	Дата	Проект: Квартира 58 м²			
Дизайнер	Кырлан А.С.			14.11.26				
Проверил					Визуализация санузла	Стадия	Лист	Листов
Н. контр.								
Утв.						П	9	92

выпуск 14.11.2026 № 2b6bd7c078 · стр. 9 из 92



	Лист	№ док.	Подпись	Дата	Проект: Квартира 58 м²			
Дизайнер	Кырлан А.С.			14.11.26				
Проверил					Визуализация прихожей	Стадия	Лист	Листов
Н. контр.								
Утв.						П	10	92

выпуск 14.11.2026 № 2b6bd7c078 · стр. 10 из 92



	Лист	№ док.	Подпись	Дата	Проект: Квартира 58 м²			
Дизайнер	Кырлан А.С.			14.11.26				
Проверил					Визуализация гардеробной	Стадия	Лист	Листов
Н. контр.								
Утв.						П	11	92

выпуск 14.11.2026 № 2b6bd7c078 · стр. 11 из 92

Список листов

Лист	Наименование
1	Титульный лист
2	Ваш проект на одной странице
3	Визуализация кухни-гостиной
4	Визуализация кухни-гостиной
5	Визуализация кухни-гостиной
6	Визуализация спальни
7	Визуализация ванной
8	Визуализация ванной
9	Визуализация санузла
10	Визуализация прихожей
11	Визуализация гардеробной
12	Список листов
13	Как читать альбом
14	План планировки от заказчика
15	План монтажный
16	Кухня (пом. 1). Монтажная схема
17	Шкафы. Монтажная схема
18	Карта покрытий стен
19	Колерная карта
20	План размещения мебели и оборудования
21	Спецификация мебели и оборудования
22	Спецификация мебели и оборудования (продолжение)
23	Спецификация мебели и оборудования (продолжение)
24	Ведомости изделий, техники и фурнитуры
25	План выводов сантехники
26	Схема разводки водопровода и канализации
27	Аксонометрическая схема В1 (холодное водоснабжение)
28	Аксонометрическая схема Т3 (горячее водоснабжение)
29	Аксонометрическая схема К1 (канализация)
30	Развёртки мокрых зон: выводы ВК. Кухня-гостиная
31	Развёртки мокрых зон: выводы ВК. Ванная
32	Развёртки мокрых зон: выводы ВК. Санузел
33	Спецификация сантехнического оборудования
34	Раскладка плитки. Ванная. Развёртки стен
35	Раскладка плитки. Санузел. Развёртки стен
36	План размещения дверей
37	Ведомость заполнения проёмов
38	План потолков
39	Разрезы и узлы потолков
40	Разрезы и узлы потолков (продолжение)
41	Однолинейная схема щита
42	Таблица нагрузок щита
43	План принципиальных трасс
44	План розеток и электровыводов
45	План слаботочных сетей
46	План освещения
47	Техническое задание на подбор светильников
48	Управление светильниками
49	План вентиляции
50	План отопления
51	План покрытий пола
52	Раскладка плитки. Планы полов
53	Раскладка плитки. Прихожая
54	Развёртка стены В. Кухня-гостиная (пом. 1), кухонный фронт
55	Развёртка стены А. Кухня-гостиная (пом. 1)
56	Развёртка стены Б. Кухня-гостиная (пом. 1)
57	Развёртка стены Г. Кухня-гостиная (пом. 1)
58	Развёртка стены А. Спальня (пом. 2)
59	Развёртка стены Б. Спальня (пом. 2)
60	Развёртка стены В. Спальня (пом. 2)
61	Развёртки стен А, Б. Ванная (пом. 3)
62	Развёртки стен В, Г. Ванная (пом. 3)
63	Развёртки стен А, Б. Санузел (пом. 4)
64	Развёртки стен В, Г. Санузел (пом. 4)
65	Развёртка стены А. Прихожая (пом. 5)
66	Развёртка стены Б. Прихожая (пом. 5)
67	Развёртка стены В. Прихожая (пом. 5)
68	Развёртка стены Г. Прихожая (пом. 5)
69	Развёртки стен А, Б. Гардеробная (пом. 6)
70	Развёртка стены Г. Гардеробная (пом. 6)
71	Открытые вопросы, принятые допущения и конфликты. Лист 1 из 2
72	Открытые вопросы, принятые допущения и конфликты. Лист 2 из 2
Д1	Шкаф-купе М-15
Д2	Система хранения М-16
Д3	Кухня (пом. 1). Развёртка гарнитура
С1	Ведомость отделки помещений
С2	Спецификация отделочных материалов
С3	Список покупок
С4	Список покупок (окончание)
С5	Смета проекта: этапы, помещения, итог
С6	Смета проекта: этапы, помещения, итог (продолжение)
С7	Смета проекта: этапы, помещения, итог (окончание)
С8	Смета материалов с ценами
С9	Смета материалов с ценами (продолжение)
С10	Смета материалов с ценами (продолжение)
С11	Смета материалов с ценами (окончание)
С12	Узлы
С13	Календарный график работ и закупок
С14	Чек-лист приёмки по этапам. Лист 1 из 3
С15	Чек-лист приёмки по этапам. Лист 2 из 3
С16	Чек-лист приёмки по этапам. Лист 3 из 3
С17	Лист → мастер

1. Размеры даны в мм от чистовых поверхностей стен: слой штукатурки 20 мм по блоку и 5 мм шпаклёвки по ГКЛ учтён. Перед заказом встроенной мебели — контрольный обмер после штукатурки.
2. Привязки мебели — от стен и углов помещения, а не от другой мебели.
3. Розетки, выводы и выключатели под мебель — см. лист 44 «План розеток и электровыводов»; сантехприборы и выводы воды — лист 25.
4. План расстановки не является документацией для изготовления мебели: изделия — по чертежам мебельщика; покупную мебель заменять только на изделия не больше габарита из спецификации (лист 21).
5. Встроенная мебель «стена в стену» — с зазором 10 мм с каждой стороны или с компенсаторами.
6. Развёртки — вид на стену изнутри помещения, по часовой стрелке; расположение стен на схеме листа развёртки; размеры — в мм по чистовым поверхностям; отметки — в м от ±0,000; высоты Н — от чистого пола помещения до оси изделия, у декора — до центра.
7. Красная цепочка — привязки электроточек и выводов по осям от угла чистовых стен; высота Н — у знака, от чистого пола до оси; высоты мебели, проёмов и границ отделки колонкой отметок слева. У знака — короткая марка; назначение, группа щита, высота и привязка каждой точки и вывода — в «Ведомости точек и выводов» под видами (каждая точка — строка).
8. У знака электроточки: марка (Р — розетка, S — выключатель, Св — светильник, ЭВ вывод кабеля), ×N — число постов в рамке, гр. — группа щита, Н — высота оси от чистого пола, мм; группы по клавишам выключателя — на листе выключателей.
9. Схема мебели, приборов и декора не является технической документацией для производства мебели; габариты — по паспортам изделий.
10. Марки позиций: М-NN — мебель, ОБ-NN — оборудование, С-NN — сантехника; О-N отделка (ведомость отделочных материалов, серия С).
11. Размеры мебели и изделий на заказ уточнить по месту после отделочных работ.

	Лист	№ док.	Подпись	Дата	Проект: Квартира 58 м²			
Дизайнер	Кырлан А.С.			14.11.26	Список листов	Стадия	Лист	Листов
Проверил						П	12	92
Н. контр.								
Утв.								

выпуск 14.11.2026 № 2b6bd7c078 · стр. 12 из 92

Общие указания

Что в альбоме

Альбом — дизайн-проект с рабочими чертежами для ремонта. Листы идут в порядке работ: титул и вводные, реестр открытых вопросов и решений, планы (обмер, монтаж стен, мебель, двери, потолки, полы), инженерия (сантехника, электрика, вентиляция и отопление), развёртки стен с визуализациями помещений, чертежи мебели, ведомости материалов и узлы.

Вам как заказчику — титул, эта вводная, «Ваш проект на одной странице», реестр вопросов, план мебели, визуализации и развёртки, ведомости мебели и материалов. Подрядчику — всё остальное: монтажные планы, привязки выводов и розеток, узлы, ведомости объёмов.

Знаки на листах

Без знака — решение утверждено или подтверждено обмером.

Что проверить до ремонта

1. Розетки у кровати и рабочего места: хватает ли их с каждой стороны кровати и над столом (план розеток — лист 44).

2. Выводы под технику — варочная панель, духовка, посудомойка, стиральная машина, бойлер: совпадают ли с выбранными моделями (листы 21, 22, 23, 44).

3. Высоты розеток, выключателей и выводов даны от чистого пола: если мебель или техника будут другими — скажите до штробления стен.

Номера записей

К-N — открытый вопрос: чего не хватает или что выбрать (варианты и рекомендация — в тексте). Пока ответа нет, действует строка «если решения нет».

Кф-N — конфликт между разделами (например, мебель и радиатор в одном месте); закрывается решением, которое записывается как ИЗ-N.

ИЗ-N — изменение проекта: что было, что стало и кто утвердил. Изменение без подписи предложение.

Все записи — на листе реестра сразу после вводных; на других листах на них стоят ссылки.

Почему альбом предварительный

Обмера на объекте не было: размеры взяты с плана заказчика. Технические условия (мощность, вода, вентиляция дома) не получены, часть решений ждёт вашего ответа. Пока в реестре есть открытые вопросы, альбом предварительный — пометка в штампе снимается закрытием вопросов, а не стиранием.


Правку к любому листу можно оставить по кнопке «Правка к листу» или на сайте студии: дизайн-студия-квартир.рф — укажите номер листа и что изменить.

3 круга правок входят в цену; условия — в договоре и на странице вашего заказа на сайте студии.

Шифр проекта ГД-2026-006-АИ

	Лист	№ док.	Подпись	Дата	Проект: Квартира 58 м²			
Дизайнер	Кырлан А.С.			14.11.26	Как читать альбом	Стадия	Лист	Листов
Проверил						П	13	92
Н. контр.								
Утв.								

выпуск 14.11.2026 № 2b6bd7c078 · стр. 13 из 92

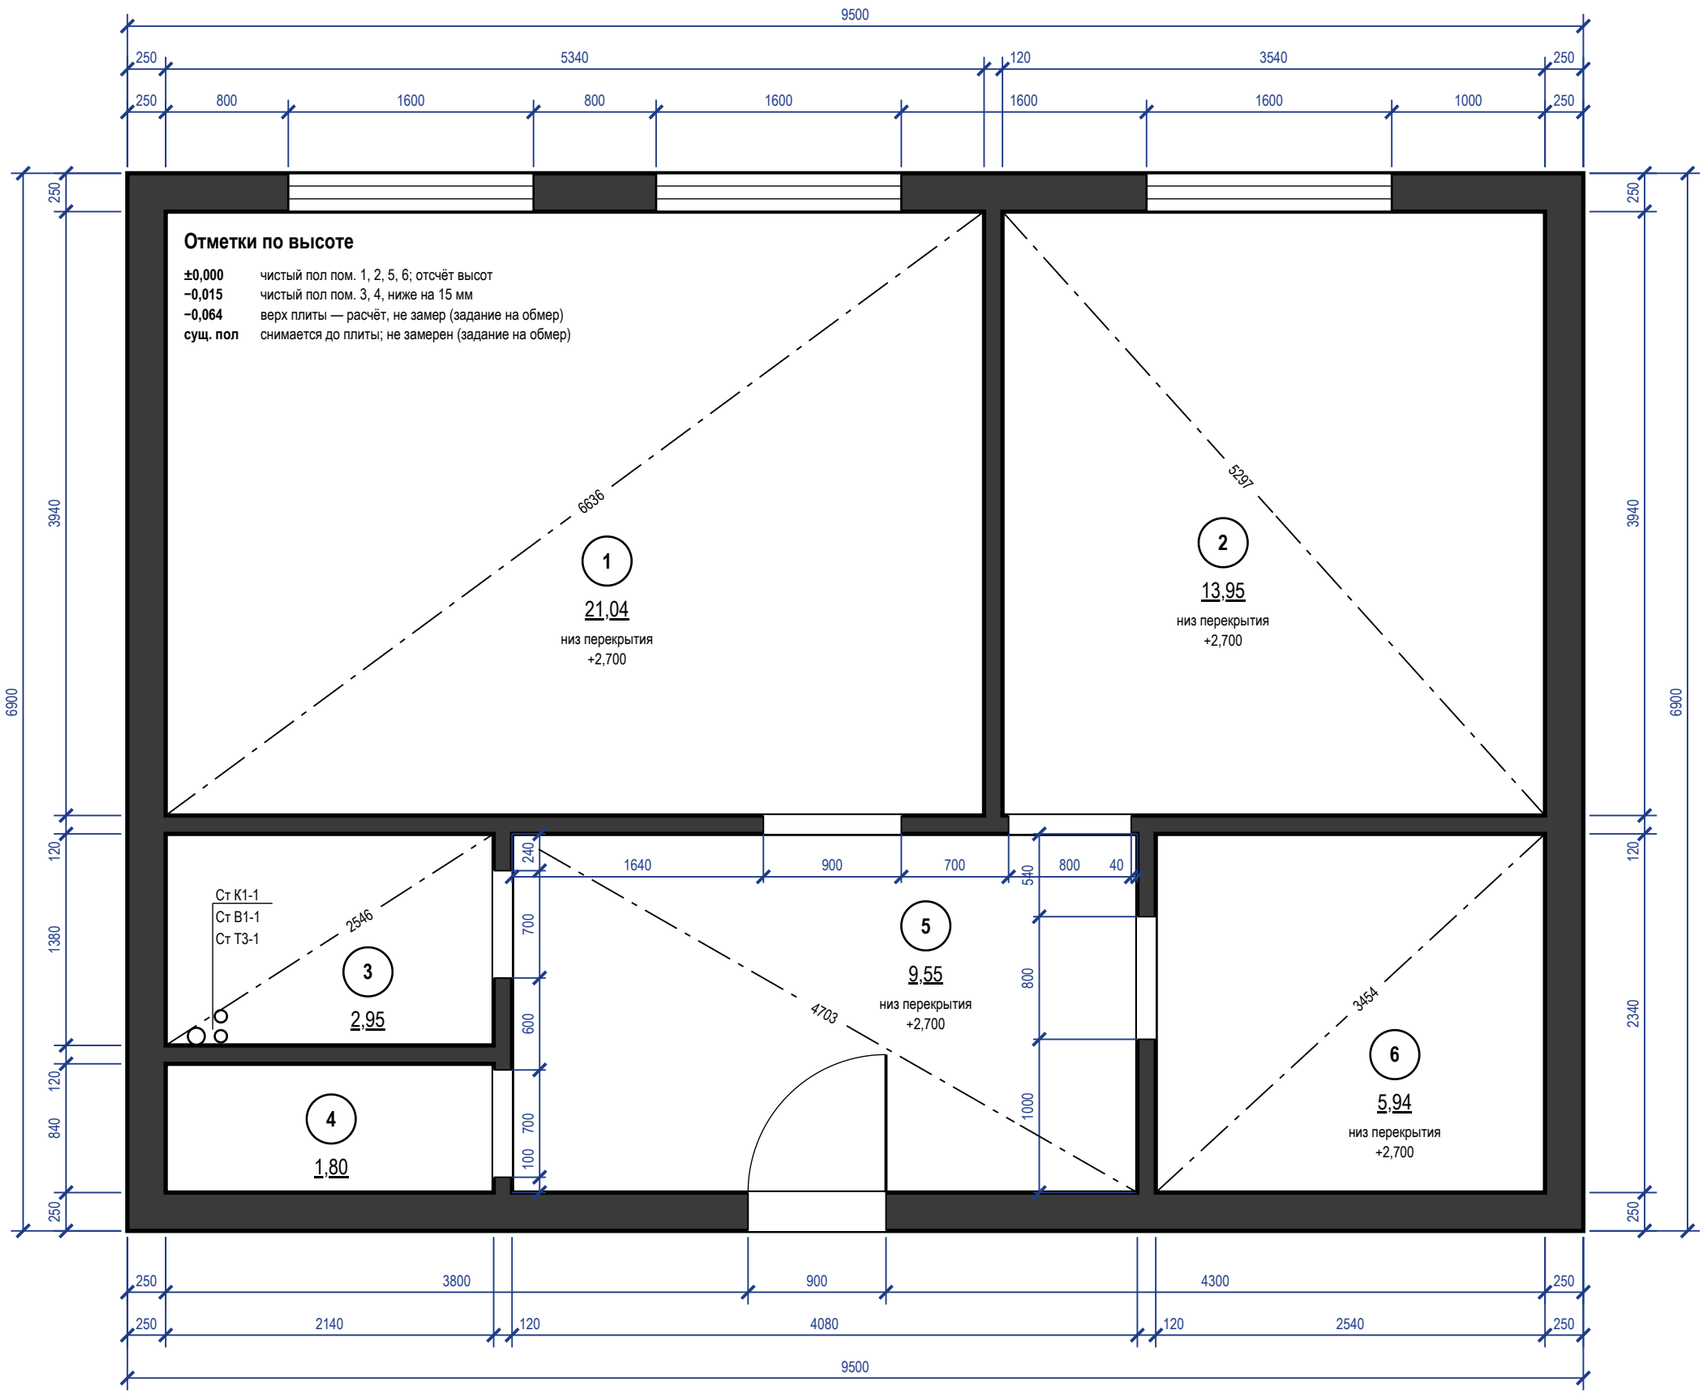

Экспликация помещений

№	Наименование	Площадь, м²
1	Кухня-гостиная	21,04
2	Спальня	13,95
3	Ванная	2,95
4	Санузел	1,80
5	Прихожая	9,55
6	Гардеробная	5,94
	Итого (общая площадь)	**55,23**

Условные обозначения

- существующие стены (сечение)
- окно (рама, остекление)
- проём существующий, без заполнения (откосы)
- стояк: К1 — канализация, В1 — ХВС, Т3 — ГВС
- диагональ помещения — контроль прямоугольности
- (1) номер помещения, площадь м²

Примечания

1. Размеры — в мм по чистым поверхностям стен до отделки (по плану заказчика); площади — в м² по тем же размерам. До начала работ выполнить контрольный обмер.
2. За отметку ±0,000 принят чистый пол, не существующий (блок отметок). «Низ перекрытия» у марки помещения — отметка низа перекрытия от ±0,000, как на развёртках и плане потолков (не высота потолка: потолок — по плану потолков).
3. Толщины стен: наружные 250 мм, перегородки 120 мм; отличающиеся толщины и уступы — размерами на плане.
4. Несущие стены не определены: до технического заключения все стены считать несущими; проёмы и штробы в них не выполнять.
5. Дверные проёмы показаны без заполнения (двери — лист 37); высота дверных проёмов 2100 мм; низ окон (подоконник) 800 мм от чистого пола, высота окон 1600 мм.
6. Диагонали — контрольные размеры; расхождение более 5 мм подписать на плане как перекос.
7. Размеры проверить на месте до начала работ; расхождение контрольных промеров ≤ 2 %.


	Лист	№ док.	Подпись	Дата
Дизайнер	Кырлан А.С.			14.11.26
Проверил				
Н. контр.				
Утв.				

Проект: Квартира 58 м² — **М 1:40**

План планировки от заказчика

Стадия	Лист	Листов
П	14	92

выпуск 14.11.2026 № 2b6bd7c078 · стр. 14 из 92

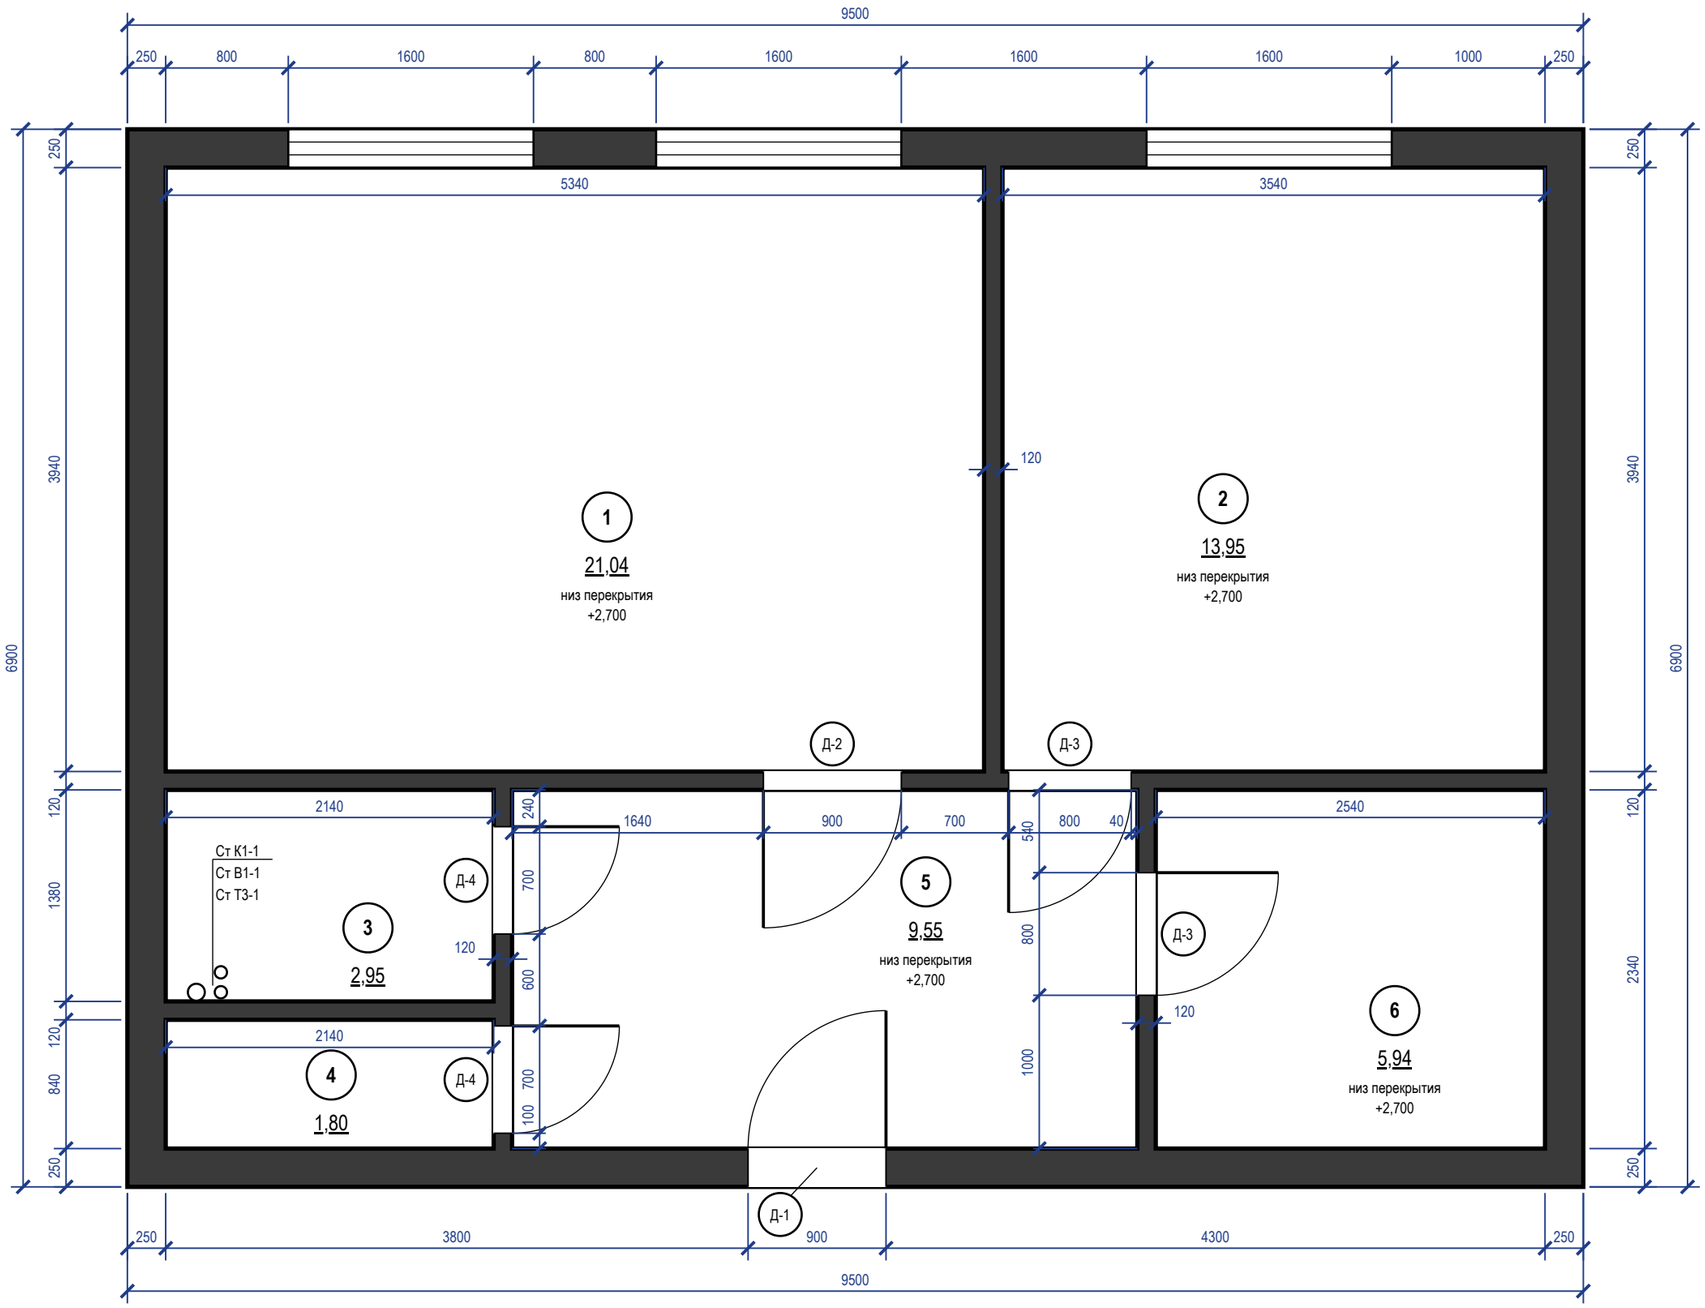

Экспликация помещений

№	Наименование	Площадь, м²
1	Кухня-гостиная	21,04
2	Спальня	13,95
3	Ванная	2,95
4	Санузел	1,80
5	Прихожая	9,55
6	Гардеробная	5,94
	Итого (общая площадь)	**55,23**

Таблица проёмов

Марка	Наименование	Проём ш×в, мм	Полотно (расч.)
Д-1	Дверь входная	900×2100	блок — задать
Д-2	Дверь скрытого монтажа	900×2100	800×2000
Д-3	Дверь скрытого монтажа	800×2100	700×2000
Д-4	Дверь скрытого монтажа	700×2100	600×2000

Примечания

1. Размеры — в мм от чистовых поверхностей стен до отделки; размеры уточнить по месту до начала работ.
2. Д-N, ПР-N в кружке — марка проёма: проём и полотно — по таблице проёмов, «расч.» — полотно по проёму, заказ — по выбранной модели; ведомость, отделка и фурнитура — лист 37.
3. Несущие стены не изменять: проёмы, ниши и штробы в них — только по техническому заключению.
4. «расч.» — полотно, выведенное из проёма по запасу каталогов; заказ — по таблице проёмов выбранной модели; Д-2, Д-3, Д-4: проём 2100, а под полотно 2000 по каталогам нужен 2050–2080, под 2100 — 2150–2180: высоту проёма — по модели; Д-1: входной блок по ГОСТ 31173-2016 — задать при выборе блока.

	Лист	№ док.	Подпись	Дата
Дизайнер	Кырлан А.С.			14.11.26
Проверил				
Н. контр.				
Утв.				


Проект: Квартира 58 м² — **М 1:40**

План монтажный


Стадия	Лист	Листов
П	15	92

выпуск 14.11.2026 № 2b6bd7c078 · стр. 15 из 92

Привязка выводов и крепление модулей (М 1:20)

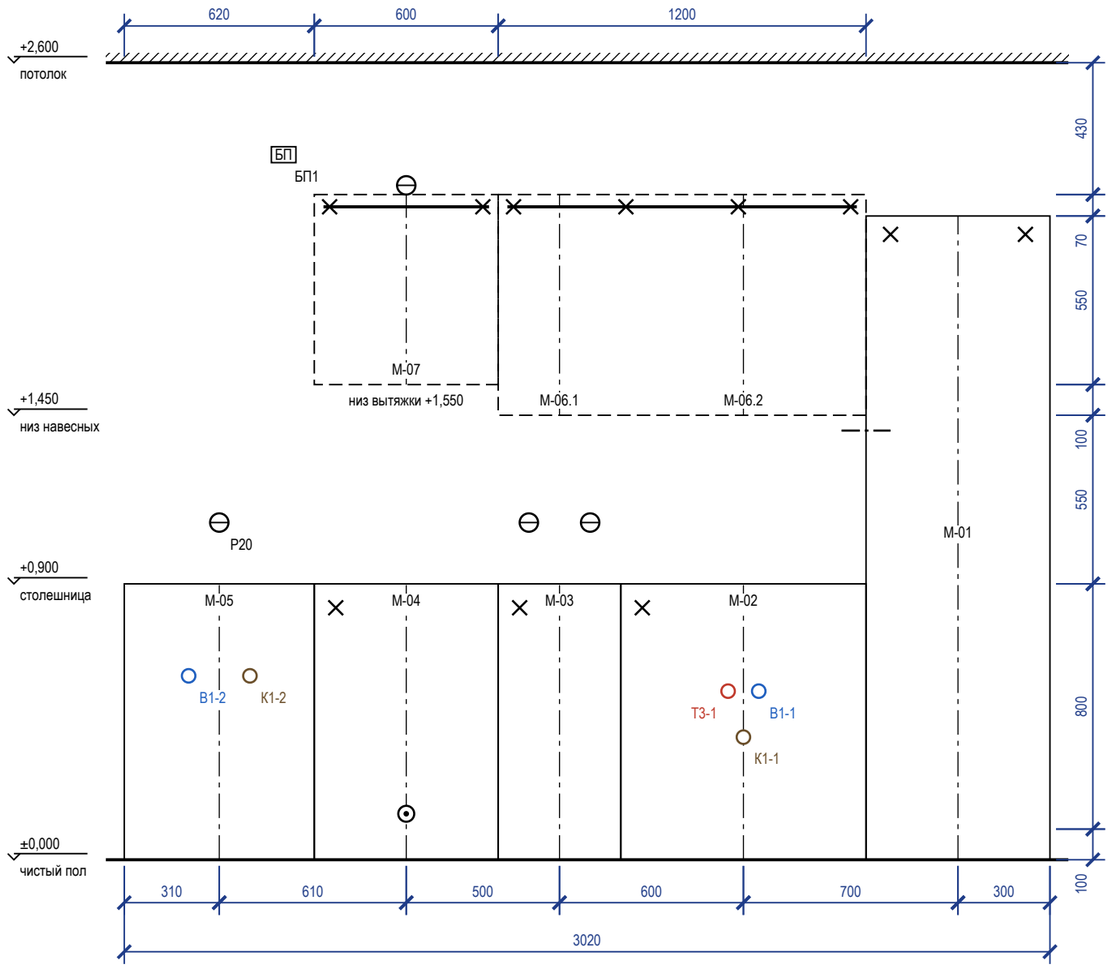

План столешницы (М 1:20)

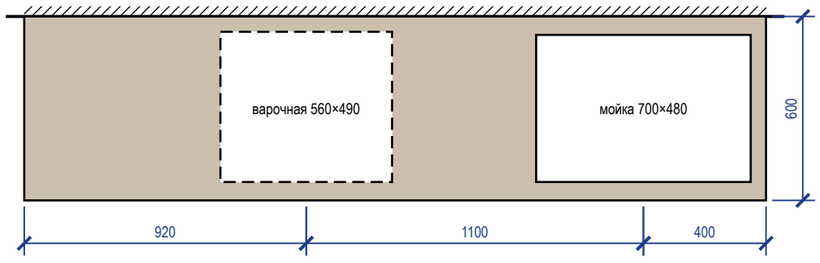

Примечания

1. Выводы — по проекту электрики и ВК; привязка по горизонтали — от оси модуля (плюс — вправо по виду), по высоте — от чистого пола до оси вывода.
2. Пенал — уголки к стене 2 шт. сверху; нижние модули — стяжками между собой и уголком к стене; ряд выставить по уровню опорами цоколя.
3. Розетки над столешницей — не ниже 150 мм над ней и не за корпусом техники; розетка за ПММ, духовым шкафом и холодильником — только в соседнем модуле или в зоне цоколя с доступом.
4. Столешница — вырезы по шаблонам выбранных моделей мойки и варочной панели; торцы у стены — герметик, пристеночный плинтус.

Привязка выводов к осям модулей

Код	Назначение	Модуль	От оси, мм	Н, мм	Размещение
В1-2	В1 — кран машины	М-05	−100	600	в нише стиральной машины, за машиной (доступ — выдвинуть машину)
Р20	розетка — стиральная машина	М-05	0	1100	над столешницей (фартук)
К1-2	К1 Ø40 — стиральная машина	М-05	+100	600	в нише стиральной машины, за машиной (доступ — выдвинуть машину)
БП1	блок питания	М-05	+210	2300	над столешницей (фартук)
	вывод кабеля — варочная панель	М-04	0	150	в соседнем модуле, за ящиком
	розетка — вытяжка (встроена в дно М-07)	М-07	0	2200	в навесном модуле
	розетка — рабочая зона	М-03	−100	1100	над столешницей (фартук)
	розетка ×2 — рабочая зона	М-03	+100	1100	над столешницей (фартук)
Т3-1	Т3 — межос. 100	М-02	−50	550	в модуле мойки
К1-1	К1 Ø50 — мойка	М-02	0	400	в модуле мойки
В1-1	В1 — межос. 100	М-02	+50	550	в модуле мойки
	светодиодная лента — подсветка столешницы	М-01	−300	1400	за пеналом

Зазоры под отделку

Поверхность	Отделка	Зазор, мм	Учесть
фартук	плитка / стеновая панель	10	от чернового основания до корпуса навесных и столешницы
стены	окраска	5	под штукатурку и шпаклёвку за пеналом
пол	инженерная доска		цоколь — после укладки пола, опоры ±20 мм


Условные обозначения

- нижний модуль, пенал (контур)
- невидимый контур: навесной модуль, корпус под столешницей
- ось модуля (от неё — привязка вывода)
- анкер / уголок крепления к стене
- розетка на стене
- вывод кабеля к технике
- В1 — вывод воды В1 / Т3, канализации К1


	Лист	№ док.	Подпись	Дата	Проект: Квартира 58 м²	М 1:20
Дизайнер	Кырлан А.С.			14.11.26	Кухня (пом. 1). Монтажная схема	Стадия: П; Лист: 16; Листов: 92
Проверил						
Н. контр.						
Утв.						

выпуск 14.11.2026 № 2b6bd7c078 · стр. 16 из 92

Шкаф-купе М-15 (пом. 5) (М 1:25)

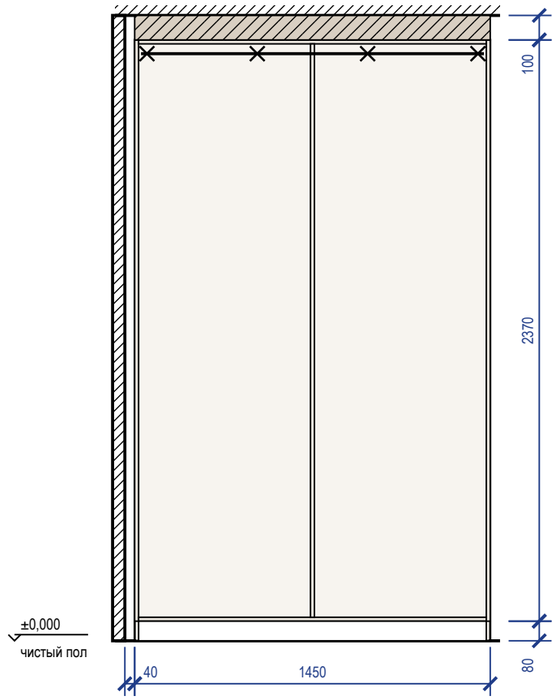

Система хранения М-16 (пом. 6) (М 1:25)

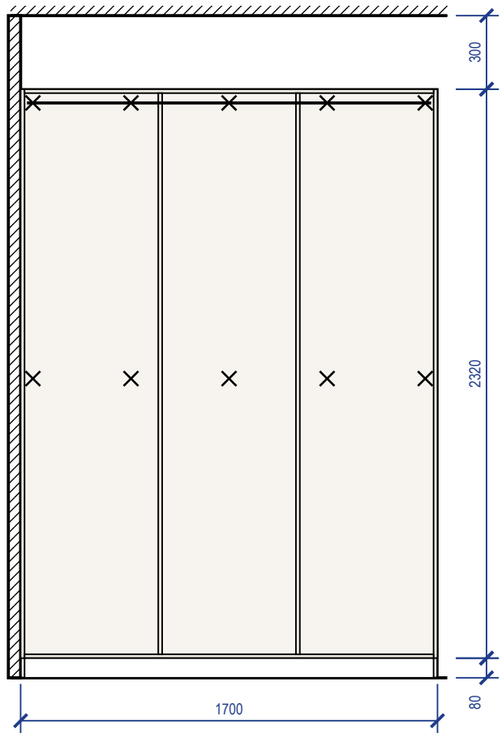

Крепление и зазоры под отделку

Марка	Помещение, стена	Основание	Отделка стены	Зазор, мм	Крепёж по планке	От опрокидывания
М-15	Прихожая (5), стена В	по основанию — см. таблицу крепежа	окраска	5	анкер 4 шт., шаг 450	уголки 2 шт.
М-16	Гардеробная (6), стена Б	по основанию — см. таблицу крепежа	окраска	5	анкер 10 шт. (2 ряда)	крепление к стене, 3 точки

Крепёж по основанию стены

Основание стены	Крепёж
бетон, ж/б	анкер-шуруп 7,5×72 или дюбель 8×60 с шурупом 5×70
кирпич полнотелый	дюбель 8×80 с шурупом 5×90
газобетон, пазогребень	дюбель для газобетона 10×100 или химический анкер
гипсокартон	закладная до обшивки (брус 40×80 или фанера 18 мм), саморез в закладную

Условные обозначения


- × — анкер / уголок крепления к стене
- корпус и полки ЛДСП (вид на стену)
- компенсатор — короб до потолка

Примечания

1. Установочные размеры — от чистого пола и чистых стен; перед установкой контрольный замер после отделки.
2. Порядок: корпус выставить по уровню опорами цоколя → закрепить к стене по задней планке → навесить двери и фасады, отрегулировать зазоры → подогнать и закрепить компенсатор.
3. Анкеры — с шагом не более 500 мм, не ближе 50 мм от края планки; на ГКЛ только в закладную, установленную до обшивки.
4. Скрытые коммуникации под анкеры проверить детектором; трассы электрики по плану розеток.

	Лист	№ док.	Подпись	Дата	Проект: Квартира 58 м²	М 1:25		
Дизайнер	Кырлан А.С.			14.11.26	Шкафы. Монтажная схема	Стадия	Лист	Листов
Проверил						П	17	92
Н. контр.								
Утв.								

выпуск 14.11.2026 № 2b6bd7c078 · стр. 17 из 92

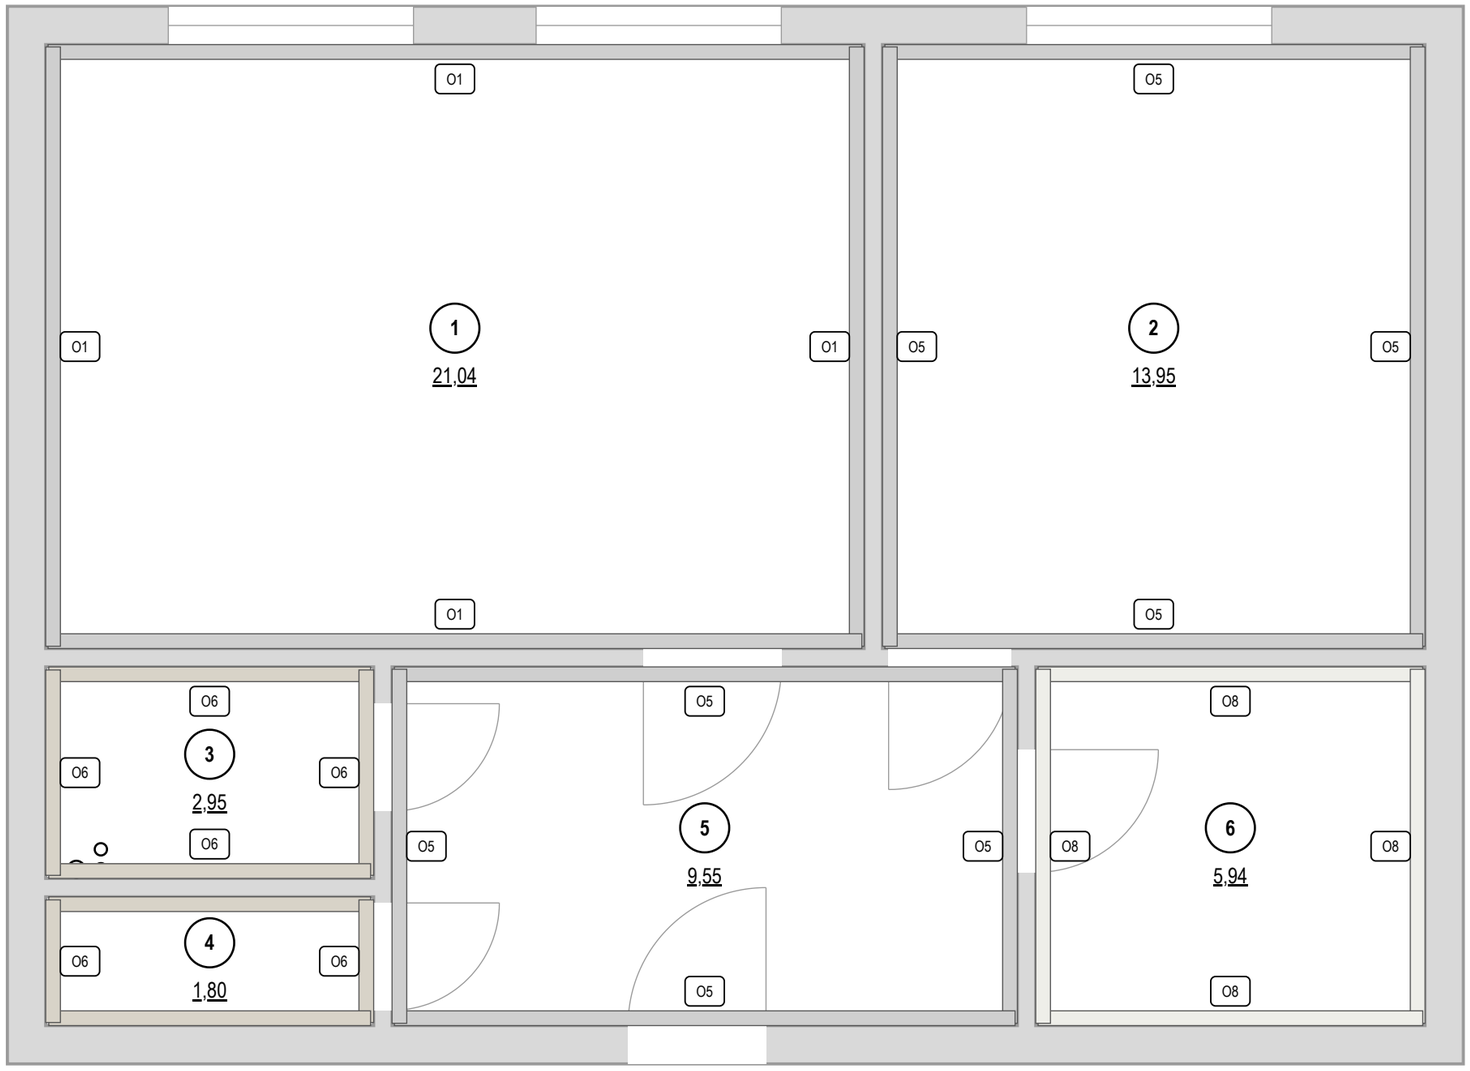

Покрытия стен

Марка	Покрытие	Помещение: S, м²	Итого, м²
O1	окраска Tikkurila · S 1002-Y50R	1: 40,9	40,9
O5	окраска Tikkurila · S 1502-Y50R	2: 34,3; 5: 22,4	56,7
O6	облицовка плиткой Italon · 610015000370 «Charme Extra» 600×1200 мм	3: 16,5; 4: 13,7	30,2
O8	окраска Tikkurila · V503 «Winter»	6: 24,3	24,3

Площади — нетто, по развёрткам (за вычетом проёмов и фартука); высоты помещений — от чистого пола.

	Лист	№ док.	Подпись	Дата
Дизайнер	Кырлан А.С.			14.11.26
Проверил				
Н. контр.				
Утв.				

Проект: Квартира 58 м² — **М 1:40**

Карта покрытий стен

Стадия	Лист	Листов
П	18	92

выпуск 14.11.2026 № 2b6bd7c078 · стр. 18 из 92

Колерная карта по помещениям

Помещение	Поверхность	Образец	Поз.	Система и код цвета	Производитель, линейка / материал, артикул	Блеск	Класс истирания	LRV	Площадь
1. Кухня-гостиная 21,04 м²	стены		**K1**	NCS S 1002-Y50R	Tikkurila	полуматов.	1	82	41,2 м²
	потолок		**K2**	NCS S 0300-N	Tikkurila	глубокомат.	1	92	21,0 м²
	пол		**KM1**	по образцу	инженерная доска · аналог по хар.				21,0 м²
	плинтус		**K3**	NCS S 0300-N	Orac Decor · Luxxus	полуматов.		92	17,7 м
2. Спальня 13,95 м²	стены		**K4**	NCS S 1502-Y50R	Tikkurila	глубокомат.	2	72	33,9 м²
	потолок		**K5**	NCS S 0300-N	Tikkurila	глубокомат.	2	92	13,9 м²
	пол		**KM1**	по образцу	инженерная доска · аналог по хар.				13,9 м²
	плинтус		**K3**	NCS S 0300-N	Orac Decor · Luxxus	полуматов.		92	14,2 м
3. Ванная 2,95 м²	стены		**KM2**	Charme Extra	Italon · арт. 610015000370				16,9 м²
	потолок		**K2**	NCS S 0300-N	Tikkurila	глубокомат.	1	92	3,0 м²
	пол		**KM3**	Две Венеции / Риальто	Kerama Marazzi · арт. SG651622R				3,0 м²
4. Санузел 1,8 м²	стены		**KM2**	Charme Extra	Italon · арт. 610015000370				14,1 м²
	потолок		**K2**	NCS S 0300-N	Tikkurila	глубокомат.	1	92	1,8 м²
	пол		**KM3**	Две Венеции / Риальто	Kerama Marazzi · арт. SG651622R				1,8 м²
5. Прихожая 9,55 м²	стены		**K6**	NCS S 1502-Y50R	Tikkurila	полуматов.	1	72	22,7 м²
	потолок		**K2**	NCS S 0300-N	Tikkurila	глубокомат.	1	92	9,6 м²
	пол		**KM3**	Две Венеции / Риальто	Kerama Marazzi · арт. SG651622R				9,6 м²
	плинтус		**K3**	NCS S 0300-N	Orac Decor · Luxxus	полуматов.		92	8,0 м
6. Гардеробная 5,94 м²	стены		**K7**	Tikkurila V503	Tikkurila · Harmony	матовая	1	86	24,7 м²
	потолок		**K8**	Tikkurila V503	Tikkurila · Anti-Reflex 2	глубокомат.	2	86	5,9 м²
	пол		**KM1**	по образцу	инженерная доска · аналог по хар.				5,9 м²
	плинтус		**K9**	Tikkurila V503	Orac Decor · Luxxus			86	9,0 м

Перечень выкрасов на согласование

№	Код	Бренд / веер	Пом. / стена	Подложка	Формат	Статус
1	S 1002-Y50R	NCS Tikkurila	1	ГКЛ с грунтом	600×1000	к выполнению
2	S 0300-N	NCS Tikkurila	1, 2, 3, 4, 5	ГКЛ с грунтом; МДФ под эмаль	600×1000; 300×600	к выполнению
3	S 1502-Y50R	NCS Tikkurila	2, 5	ГКЛ с грунтом	600×1000	к выполнению
4	V503	Tikkurila	6	ГКЛ с грунтом; МДФ под эмаль	600×1000; 300×600	к выполнению

Примечания

1. Цвет на листе и на экране — ориентир. До покраски — выкрас на объекте: не меньше А3 (или лист ГКЛ), на грунте под эту краску, не на белой шпаклёвке, в 2 слоя; на обороте — код, бренд, веер, дата. Смотреть днём и вечером, рядом с образцами пола и плитки; к основному цвету стен — ещё 2 соседних оттенка. Красить только в цвет утверждённого выкраса.
2. Краску заказывать по коду из графы «Система и код цвета» у бренда этого кода, не «аналогом» другого; весь объём одного кода — одной партией, колеруемую краску — за один проход машины.
3. Площади — те же, что в ведомости отделки (лист С1); сколько краски заказать — в спецификации отделочных материалов (лист С2).

Схема квартиры: цвет стен и акценты (б/м)

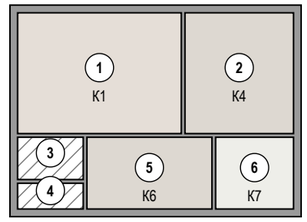


Схема палитры проекта


Стиль: Скандинавский · схема: нейтральная

основной	основной	основной	второстепенный	акцентный
NCS S 1502-Y50R	**NCS S 1002-Y50R**	**NCS S 0300-N**	**Tikkurila V503**	**NCS S 4010-R90B**
тёплый светло-серый LRV 72 стены 2,5	тёплый светлый грейж LRV 82 стены 1	белый LRV 92 потолок 1,2,3,4,5; плинтус 1,2,5	Winter LRV 86 стены 6; потолок 6; плинтус 6	пыльный синий LRV 27 текстиль/декор 1,2,3

План 60/30/10



Окраска, факт — по площади стен, акцентов, потолков

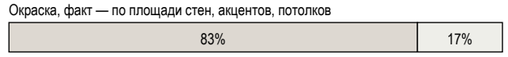

окрашено всего 177,7 м²; второстепенный тон несут мебель и текстиль

Текстиль и декор в цветах вне палитры проекта

- Tikkurila G503 Calla — пом. 1 (T1, T2, T4), 2 (T7), 3 (T13)
- NCS S 2002-Y серый камень, тёплый — пом. 1 (T3)
- NCS S 3010-G10Y шалфей средний — пом. 1 (T6), 2 (T9), 4 (ДК12)
- Farrow & Ball No. 241 Skimming Stone — пом. 2 (T8)

Условные обозначения

- **K1** NCS S 1002-Y50R · Tikkurila · полуматов. · кл. 1
- **K2** NCS S 0300-N · Tikkurila · глубокомат. · кл. 1
- **K3** NCS S 0300-N · Orac Decor Luxxus · полуматов.
- **K4** NCS S 1502-Y50R · Tikkurila · глубокомат. · кл. 2
- **K5** NCS S 0300-N · Tikkurila · глубокомат. · кл. 2
- **K6** NCS S 1502-Y50R · Tikkurila · полуматов. · кл. 1
- **K7** Tikkurila V503 · Winter · Harmony · матовая · кл. 1
- **K8** Tikkurila V503 · Winter · Anti-Reflex 2 · глубокомат. · кл. 2
- **K9** Tikkurila V503 · Winter · Luxxus
- **KM1** аналог: инженерная доска, дуб натуральный, масло, 1-полосная, 14/4 мм
- **KM2** плитка · 610015000370
- **KM3** керамогранит · SG651622R

дерево (доска, паркет, ламинат) — рисунок досок


керамогранит, плитка, камень — сетка швов по формату

плашка не залита — цвет только по коду и вееру бренда

K — краска, KM — отделочный материал (тон KM — по описанию, эталон — образец материала); кл. — класс истирания (1 — самый стойкий к мытью); LRV — светлота цвета: 0 — чёрный, 100 — белый

	Лист	№ док.	Подпись	Дата	Проект: Квартира 58 м²			
Дизайнер	Кырлан А.С.			14.11.26	Колерная карта	Стадия	Лист	Листов
Проверил						П	19	92
Н. контр.								
Утв.								

выпуск 14.11.2026 № 2b6bd7c078 · стр. 19 из 92

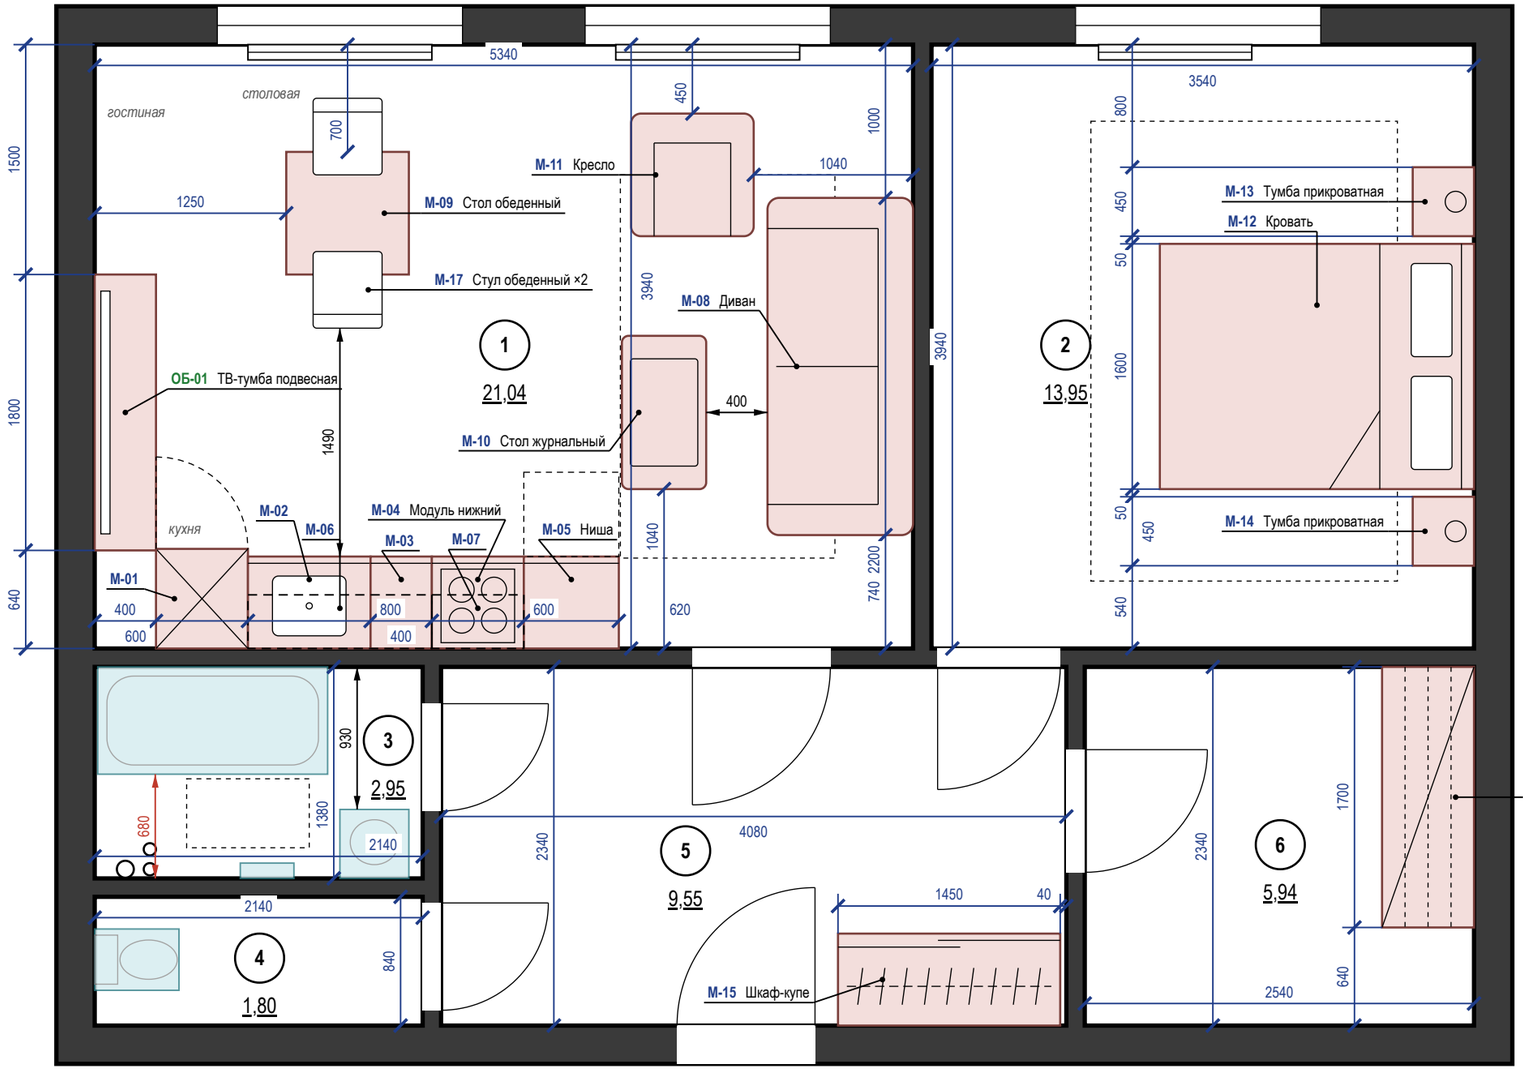

Экспликация помещений

лист 14 · на плане — номера в марках

Ведомость мебели и оборудования

Марка	Наименование	Ш×Г×В, мм	Пом.	Кол.
М-01	Пенал кухонный	600×650×2100	1	1
М-02	Модуль нижний	800×600×900	1	1
М-03	Модуль нижний	400×600×900	1	1
М-04	Модуль нижний	600×600×900	1	1
М-05	Ниша под стиральную машину	620×600×900	1	1
М-06	Модуль навесной	1200×350×720	1	1
М-07	Навесной модуль над варочной	600×350×620	1	1
М-08	Диван	2200×950×850	1	1
М-09	Стол обеденный	800×800×750	1	1
ОБ-01	ТВ-тумба подвесная с экраном	1800×400×450	1	1
М-10	Стол журнальный	550×1000×400	1	1
М-11	Кресло	800×800×800	1	1
М-12	Кровать двуспальная	1600×2050×450	2	1
М-13	Тумба прикроватная	450×400×500	2	1
М-14	Тумба прикроватная	450×400×500	2	1
М-15	Шкаф-купе	1450×600×2450	5	1
М-16	Система хранения	1700×600×2400	6	1
М-17	Стул обеденный к столу М-09	450×500×820	1	2

Ш — вдоль стены (изголовья), Г — от стены (длина кровати)

Материалы, модели, допуск замены — лист 21

Примечания

1. Размеры — в мм от чистовых поверхностей стен; габариты предметов (Ш×Г×В) — в ведомости мебели, лист 21, на плане марка и короткое имя; размеры мебели уточнить после отделочных работ; общие указания — лист 12.
2. У позиций М-01, М-02, М-03, М-06, М-07 на плане только марка: наименование и габарит — в спецификации, лист 21.
3. Стулья обеденной группы (М-17 — 2 шт.) показаны в рабочем положении, задвинутыми под столешницу на 150 мм.

	Лист	№ док.	Подпись	Дата
Дизайнер	Кырлан А.С.			14.11.26
Проверил				
Н. контр.				
Утв.				

Проект: Квартира 58 м² — **М 1:40**

План размещения мебели и оборудования

Стадия	Лист	Листов
П	20	92

выпуск 14.11.2026 № 2b6bd7c078 · стр. 20 из 92

Поз.	Наименование и техническая характеристика	Тип, марка, обозначение документа, опросного листа	Код продукции	Поставщик	Ед. измерения	Кол.	Масса 1 ед., кг	Примечание
	Мебель встроенная и корпусная (изготовление по чертежам мебельщика)							
М-01	Пенал кухонный, холодильник; корпус ЛДСП 16 мм; фасады — без фасада (прибор отдельностоящий); Ш×Г×В 600×650×2100 мм	—	—	изготовление на заказ	шт.	1	—	пом. 1
М-02	Модуль нижний, мойка; корпус ЛДСП 16 мм; фасады — МДФ эмаль 18 мм; Ш×Г×В 800×600×900 мм	—	—	изготовление на заказ	шт.	1	—	пом. 1
М-03	Модуль нижний; корпус ЛДСП 16 мм; фасады — МДФ эмаль 18 мм; Ш×Г×В 400×600×900 мм	—	—	изготовление на заказ	шт.	1	—	пом. 1
М-04	Модуль нижний, варочная; корпус ЛДСП 16 мм; фасады — МДФ эмаль 18 мм; Ш×Г×В 600×600×900 мм	—	—	изготовление на заказ	шт.	1	—	пом. 1
М-05	Модуль под встраиваемую ПММ 60; без корпуса (ниша между соседними модулями); фасад на дверь машины — МДФ эмаль 18 мм; цоколь; Ш×Г×В 620×600×900 мм	—	—	изготовление на заказ	шт.	1	—	пом. 1
М-06	Модуль навесной; корпус ЛДСП 16 мм; фасады — МДФ эмаль 18 мм; Ш×Г×В 1200×350×720 мм	—	—	изготовление на заказ	шт.	1	—	пом. 1
М-07	Навесной модуль над варочной, вытяжка встраивается в дно; корпус ЛДСП 16 мм; фасады — МДФ эмаль 18 мм; Ш×Г×В 600×350×620 мм	—	—	изготовление на заказ	шт.	1	—	пом. 1
М-15	Шкаф-купе; корпус ЛДСП 16 мм; фасады — ЛДСП 10 мм в алюминиевом профиле; Ш×Г×В 1450×600×2450 мм	—	—	изготовление на заказ	шт.	1	—	пом. 5
М-16	Система хранения: штанги, полки, ящики; каркас и полки — ЛДСП 16 мм, декор «дуб натуральный»; без фасадов; Ш×Г×В 1700×600×2400 мм	—	—	изготовление на заказ	шт.	1	—	пом. 6; крепление к стене
	Мебель покупная							
М-08	Диван; обивка — ткань, цвет Tikkurila V503; Ш×Г×В 2200×950×850 мм	аналог: Ш×Г×В 2200×950×850 мм, обивка — ткань	—	аналог по характеристикам	шт.	1	—	пом. 1; замена ≤ габарита
М-09	Стол обеденный; шпон, дуб натуральный, матовое масло; Ш×Г×В 800×800×750 мм	аналог: Ш×Г×В 800×800×750 мм, шпон	—	аналог по характеристикам	шт.	1	—	пом. 1; замена ≤ габарита
М-10	Стол журнальный; шпон, дуб натуральный, матовое масло; Ш×Г×В 550×1000×400 мм	аналог: Ш×Г×В 550×1000×400 мм, шпон	—	аналог по характеристикам	шт.	1	—	пом. 1; замена ≤ габарита
М-11	Кресло; обивка — ткань, цвет Tikkurila V503; Ш×Г×В 800×800×800 мм	аналог: Ш×Г×В 800×800×800 мм, обивка — ткань	—	аналог по характеристикам	шт.	1	—	пом. 1; замена ≤ габарита
М-17	Стул обеденный к столу М-09; обивка — ткань, цвет Tikkurila V503; каркас — дуб натуральный; Ш×Г×В 450×500×820 мм	аналог: Ш×Г×В 450×500×820 мм, обивка — ткань	—	аналог по характеристикам	шт.	2	—	пом. 1; замена ≤ габарита
ОБ-01	ТВ-тумба подвесная с экраном; шпон, дуб натуральный, матовое масло; Ш×Г×В 1800×400×450 мм	аналог: Ш×Г×В 1800×400×450 мм, шпон	—	аналог по характеристикам	шт.	1	—	пом. 1; замена ≤ габарита
М-12	Кровать двуспальная; мягкое изголовье, обивка — ткань, цвет Tikkurila V503; Ш×Г×В 1600×2050×450 мм	аналог: Ш×Г×В 1600×2050×450 мм, мягкое изголовье	—	аналог по характеристикам	шт.	1	—	пом. 2; замена ≤ габарита
М-13, М-14	Тумба прикроватная; шпон, дуб натуральный, матовое масло; Ш×Г×В 450×400×500 мм	аналог: Ш×Г×В 450×400×500 мм, шпон	—	аналог по характеристикам	шт.	2	—	пом. 2; замена ≤ габарита
	Техника встраиваемая и бытовая (покупные изделия), светильники под розетки							
	Холодильник, в модуле М-01	аналог по характеристикам: отдельностоящий, габарит — по проёму	—	по выбору заказчика до изготовления мебели	шт.	1	—	пом. 1; по схеме изготовителя
	Стиральная машина, в модуле М-05	аналог по характеристикам: тип загрузки — по листу ВК, по листу ВК	—	по выбору заказчика до изготовления мебели	шт.	1	—	пом. 1; по схеме изготовителя
	Варочная панель встраиваемая, индукционная, в модуле М-04	аналог по характеристикам: индукционная 60 см, вырез 560 × 490 мм по шаблону модели	—	по выбору заказчика до изготовления мебели	шт.	1	—	пом. 1; по схеме изготовителя

Примечания

1. Позиции мебели совпадают с марками на плане расстановки; размеры Ш×Г×В — Ш вдоль стены, Г от стены.
2. Размеры и привязки плана расстановки — в мм от чистовых поверхностей стен: слой штукатурки 20 мм по блоку и 5 мм шпаклёвки по ГКЛ учтён; привязки — от стен и углов помещения, а не от другой мебели.
3. План расстановки не является документацией для изготовления мебели. Встроенная и корпусная мебель изготавливается по чертежам мебельщика после контрольного обмера (после штукатурки); «стена в стену» — с зазором 10 мм с каждой стороны или с компенсаторами; графы «Тип, марка» и «Код продукции» для неё не заполняются (ГОСТ 21.110-2013).
4. Покупные изделия — аналог по характеристикам: заменять только на изделия не больше указанного габарита и того же материала и цвета.
5. Материал и цвет, не указанные в данных изделия, приняты по концепции: тон дерева — по полу, обивка — по вторичному цвету палитры; образцы согласовать до заказа.
6. Масса 1 ед. для изделий до 25 кг не указывается. Техника — по монтажным схемам изготовителя; выводы — по листам ЭОМ и ВК.

	Лист	№ док.	Подпись	Дата
Дизайнер	Кырлан А.С.			14.11.26
Проверил				
Н. контр.				
Утв.				

Проект: Квартира 58 м²

Спецификация мебели и оборудования

Стадия	Лист	Листов
П	21	92

выпуск 14.11.2026 № 2b6bd7c078 · стр. 21 из 92

Поз.	Наименование и техническая характеристика	Тип, марка, обозначение документа, опросного листа	Код продукции	Поставщик	Ед. измерения	Кол.	Масса 1 ед., кг	Примечание
	Вытяжка встраиваемая, в модуле М-07	аналог по характеристикам: производительность — по расчёту ОВ, шум ≤ 55 дБ(А)	—	по выбору заказчика до изготовления мебели	шт.	1	—	пом. 1; по схеме изготовителя
	Кондиционер настенный (сплит-система), внутренний блок, КВ-1, стена Г, низ — (высота блока не задана, уточнить по паспорту модели) — предложено	аналог по характеристикам: настенный инверторный, 2,5 кВт, блок 900×—×250 мм, дренаж наружу, трасса фреона — по паспорту модели	—	по выбору заказчика до изготовления мебели	шт.	1	—	пом. 1; предложено, решает заказчик; по паспорту модели
	Кондиционер, наружный блок, КН-1, стена А — предложено	аналог по характеристикам: в корзине на фасаде, вынос ≤ 350 мм, доступ для обслуживания с лоджии/окна/автовышки; согласие собственников	—	по выбору заказчика до изготовления мебели	шт.	1	—	пом. 1; предложено, решает заказчик; по паспорту модели
	Кондиционер настенный (сплит-система), внутренний блок, КВ-2, стена А, низ — (высота блока не задана, уточнить по паспорту модели)	аналог по характеристикам: настенный инверторный, 2 кВт, блок 780×—×220 мм, дренаж наружу, трасса фреона — по паспорту модели	—	по выбору заказчика до изготовления мебели	шт.	1	—	пом. 2; по паспорту модели
	Кондиционер, наружный блок, КН-2, стена А	аналог по характеристикам: в корзине на фасаде, вынос ≤ 350 мм, доступ для обслуживания с лоджии/окна/автовышки; согласие собственников	—	по выбору заказчика до изготовления мебели	шт.	1	—	пом. 2; по паспорту модели
	Торшер, у поз. М-09; абажур — ткань или опаловое стекло; лампа 3000 K	—	—	аналог по характеристикам	шт.	1	—	пом. 1; розетка — по плану розеток (ЭОМ)
	Текстиль							
Т1	Портьеры — шторы льняные в пол, молочные (окно 1); лён 100 %; цвет Tikkurila G503; карниз 2100 мм, высота 2590 мм, сборка 2	—	—	аналог по характеристикам	шт.	2	—	пом. 1
Т2	Портьеры — шторы льняные в пол, молочные (окно 2); лён 100 %; цвет Tikkurila G503; карниз 2100 мм, высота 2590 мм, сборка 2	—	—	аналог по характеристикам	шт.	2	—	пом. 1
Т3	Ковёр шерстяной плоского плетения 1400×2500, овсяный; шерсть 100 %; цвет NCS S 2002-Y; 1400×2500 мм	—	—	аналог по характеристикам	шт.	1	—	пом. 1; с подложкой
Т4	Подушки на диван, букле молочное; букле (шерсть 60 %, полиэстер 40 %); цвет Tikkurila G503	—	—	аналог по характеристикам	шт.	3	—	пом. 1
Т5	Подушки на диван, лён, пыльный синий; лён 100 %; цвет NCS S 4010-R90B	—	—	аналог по характеристикам	шт.	2	—	пом. 1
Т6	Плед шерстяной на диван, шалфей; шерсть мериноса 100 %; цвет NCS S 3010-G10Y	—	—	аналог по характеристикам	шт.	1	—	пом. 1
Т7	Римская штора льняная с блэкаут-подкладкой, молочная; лён 100 %; цвет Tikkurila G503; карниз 1650 мм, высота 1750 мм	—	—	аналог по характеристикам	шт.	1	—	пом. 2
Т8	Ковёр шерстяной 2000×3000 под кроватью, светлый каменный; шерсть 100 %; цвет Farrow & Ball No. 241; 2000×3000 мм	—	—	аналог по характеристикам	шт.	1	—	пом. 2; с подложкой
Т9	Подушки декоративные на кровать, лён, шалфей; лён 100 %; цвет NCS S 3010-G10Y	—	—	аналог по характеристикам	шт.	2	—	пом. 2
Т10	Подушка-валик на кровать, букле, пыльный синий; букле (шерсть 60 %, полиэстер 40 %); цвет NCS S 4010-R90B	—	—	аналог по характеристикам	шт.	1	—	пом. 2
Т11	Плед шерстяной крупной вязки в изножье кровати, пыльный синий; шерсть мериноса 100 %; цвет NCS S 4010-R90B	—	—	аналог по характеристикам	шт.	1	—	пом. 2
Т12	Полотенца банные махровые, пыльный синий, сложены на полотенцесушителе; хлопок 100 %; цвет NCS S 4010-R90B	—	—	аналог по характеристикам	шт.	2	—	пом. 3
Т13	Полотенца для рук вафельные, молочные, на нижних перекладинах сушителя; хлопок 100 %; цвет Tikkurila G503	—	—	аналог по характеристикам	шт.	2	—	пом. 3

	Лист	№ док.	Подпись	Дата
Дизайнер	Кырлан А.С.			14.11.26
Проверил				
Н. контр.				
Утв.				

Проект: Квартира 58 м²

Спецификация мебели и оборудования (продолжение)

Стадия	Лист	Листов
П	22	92

Поз.	Наименование и техническая характеристика	Тип, марка, обозначение документа, опросного листа	Код продукции	Поставщик	Ед. измерения	Кол.	Масса 1 ед., кг	Примечание
Т14	Ковёр — коврик для ванной у бортика ванны, хлопок тафтинг, пыльный синий; хлопок 100 %, латексная противоскользящая основа; цвет NCS S 4010-R90B; 800×450 мм	—	—	аналог по характеристикам	шт.	1	—	пом. 3; с подложкой
	Декор							
ДК1	Постер над диваном, левый: графика тушью в паспарту, дубовая рама 600×800; 600×800 мм; низ на 1050 мм от пола	—	—	аналог по характеристикам	шт.	1	3	пом. 1; крепление: дюбель с крюком, 2 точки
ДК2	Постер над диваном, правый: гуашь в паспарту, дубовая рама 600×800; 600×800 мм; низ на 1050 мм от пола	—	—	аналог по характеристикам	шт.	1	3	пом. 1; крепление: дюбель с крюком, 2 точки
ДК3	Фикус каучуконосный в напольном керамическом кашпо Ø400, матовый белый; 450×450 мм	—	—	аналог по характеристикам	шт.	1	—	пом. 1
ДК4	Ваза керамическая с веткой эвкалипта на обеденном столе, матовая глазурь, пыльный синий; 200×300 мм; на М-09	—	—	аналог по характеристикам	шт.	1	—	пом. 1
ДК5	Картина над кроватью: акварель в паспарту, дубовая рама 1100×700; 1100×700 мм; низ на 1200 мм от пола	—	—	аналог по характеристикам	шт.	1	4	пом. 2; крепление: дюбель с крюком, 2 точки
ДК6	Зеркало в рост в тонкой дубовой раме 600×1600; 600×1600 мм; низ на 300 мм от пола	—	—	аналог по характеристикам	шт.	1	12	пом. 2; крепление: анкер для пустотелых оснований, 4 шт.
ДК7	Замиокулькас в напольном кашпо Ø350, керамика; 400×400 мм	—	—	аналог по характеристикам	шт.	1	—	пом. 2
ДК8	Зеркало над умывальником, влагостойкое, в тонкой дубовой раме 450×650; 450×650 мм; низ на 1150 мм от пола	—	—	аналог по характеристикам	шт.	1	5	пом. 3; крепление: клей для зеркал + 2 опорных уголка снизу
ДК9	Постер в тонкой чёрной раме 300×400: линейный рисунок; рама — чёрный матовый; 300×400 мм; центр на 1500 мм от пола	—	—	аналог по характеристикам	шт.	1	1	пом. 4; крепление: дюбель с крюком, 1 точка
ДК12	Ваза-бутыль керамическая, шалфей, с сухой веткой эвкалипта — на полке короба инсталляции; 130×400 мм	—	—	аналог по характеристикам	шт.	1	—	пом. 4
ДК13	Свеча в янтарном стекле и аромадиффузор с ротанговыми палочками на подносе — на полке короба; 150×180 мм	—	—	аналог по характеристикам	шт.	1	—	пом. 4
ДК10	Зеркало в рост в дубовой раме 600×1700; 600×1700 мм; низ на 300 мм от пола	—	—	аналог по характеристикам	шт.	1	12	пом. 5; крепление: анкер для пустотелых оснований, 4 шт.
ДК11	Постер между дверями: линогравюра, дубовая рама 400×560; 400×560 мм; центр на 1500 мм от пола	—	—	аналог по характеристикам	шт.	1	2	пом. 5; крепление: дюбель с крюком, 2 точки

	Лист	№ док.	Подпись	Дата
Дизайнер	Кырлан А.С.			14.11.26
Проверил				
Н. контр.				
Утв.				

Проект: Квартира 58 м²

Спецификация мебели и оборудования (продолжение)

Стадия	Лист	Листов
П	23	92

Ведомость изделий

Марка	Наименование	Пом.	Ш×Г×В, мм	Корпус	Фасад	Кромка, мм	Кол.
М-15	Шкаф-купе	5	1450×600×2450	ЛДСП 16	ЛДСП 10 мм в алюминиевом профиле	0,4 / 1	1
М-16	Система хранения	6	1700×600×2400	ЛДСП 16	без фасадов	0,4 / 2 *	1
М-05	Ниша под стиральную машину 620: без корпуса, между боковинами соседних модулей, фасад на петлях к боковине соседнего модуля; цоколь съёмный	1	620×600×900	без корпуса	МДФ эмаль 18 мм — на дверь машины (навеска из её комплекта), цоколь		1
М-04	Модуль нижний: ящики, варочная	1	600×600×900	ЛДСП 16	МДФ эмаль 18 мм	0,4 / 1	1
М-07	Модуль навесной: полки	1	600×350×620	ЛДСП 16	МДФ эмаль 18 мм	0,4 / 1	1
М-03	Модуль нижний: ящики	1	400×600×900	ЛДСП 16	МДФ эмаль 18 мм	0,4 / 1	1
М-06	Модуль навесной: полки, сушка	1	1200×350×720	ЛДСП 16	МДФ эмаль 18 мм	0,4 / 1	1
М-02	Модуль нижний: мойка	1	800×600×900	ЛДСП 16	МДФ эмаль 18 мм	0,4 / 1	1
М-01	Место под холодильник отдельностоящий: без корпуса и фасада	1	600×650×2100 (место в ряду)	без корпуса	без фасада (прибор отдельностоящий)		

Ведомость встраиваемой техники

Поз.	Прибор	Ниша, вырез, мм	Вентиляция	Питание	Схема
М-04	Варочная панель индукционная, 60 см	вырез в столешнице 560 × 490		М-04, H=150 — в соседнем модуле, за ящиком	по модели
М-02	Мойка врезная / подстольная с сифоном	вырез по шаблону, ориентир 700 × 480		смеситель — выводы ВК	по модели
М-01	Холодильник отдельностоящий	проём 600, зазор сверху ≥ 50	по паспорту модели	питание: точка ЭОМ не задана — вывод под прибор не делать до задания	по модели
М-07	Вытяжка встраиваемая в навесной модуль, 60 см	низ ≥ 650 над панелью	воздуховод к вентканалу, короб до потолка	питание: точка ЭОМ не задана — вывод под прибор не делать до задания	по модели

Ведомость фурнитуры

№	Фурнитура	Тип, размер	Изделия	Кол.
1	Система дверей купе: профиль, направляющие, ролики	на 2 двери	М-15	1
2	Ручка-профиль вертикальная	в цвет профиля	М-15	2
3	Полкодержатель с фиксацией	ø5 мм	М-15, М-16, М-07, М-06	56
4	Штанга овальная 30×15, L = 701	+ 2 держателя	М-15	1
5	Полка для обуви выдвижная наклонная	ширина 701	М-15	3
6	Опора регулируемая с цоколем на клипсах	ход 20 мм	М-15, М-16	14
7	Анкер по основанию стены	по таблице крепежа	М-15, М-16, М-07, М-06	20
8	Уголок крепления к стене от опрокидывания	стальной	М-15, М-16	4
9	Штанга овальная 30×15, L = 545	+ 2 держателя	М-16	3
10	Петля накладная 110° с доводчиком	чашка 35 мм	М-05, М-07, М-06, М-02	16
11	Ручка-профиль	латунь матовая	М-05, М-04, М-07, М-03, М-06, М-02	14
12	Направляющие полного выдвижения с доводчиком NL 500	пара	М-04, М-03	6
13	Опора кухонная регулируемая 100–120 мм	+ клипса цоколя	М-04, М-03, М-02	14
14	Навес регулируемый для навесного шкафа	пара на секцию	М-07, М-06	3
15	Шина монтажная	L = 540	М-07	1
16	Сушка для посуды в шкаф	ширина 800	М-06	1
17	Шина монтажная	L = 1140	М-06	1


Примечания

1. Модели техники выбирает заказчик до изготовления мебели; ниши, вырезы и вентиляция — по монтажной схеме выбранной модели (условие гарантии), её номер вносится в ведомость.
2. Количество фурнитуры — по чертежам изделий; запас крепежа 5 %. Аналоги — по характеристикам (доводчик, нагрузка, ход).
3. Цвет корпусов, фасадов и профилей — по колерной карте проекта. Кромка — скрытые / видимые торцы, мм.
4. Кромка в данных изделия не задана: принята ПВХ 0,4 мм на скрытых торцах и 2 мм на видимых (по умолчанию для ЛДСП корпуса и МДФ фасада); заказчик или мебельщик подтверждает до раскроя.


	Лист	№ док.	Подпись	Дата	Проект: Квартира 58 м²			
Дизайнер	Кырлан А.С.			14.11.26				
Проверил					Ведомости изделий, техники и фурнитуры	Стадия	Лист	Листов
Н. контр.						П	24	92
Утв.								

выпуск 14.11.2026 № 2b6bd7c078 · стр. 24 из 92


Фрагмент 1. Кухня-гостиная, пом. 1 (М 1:25)

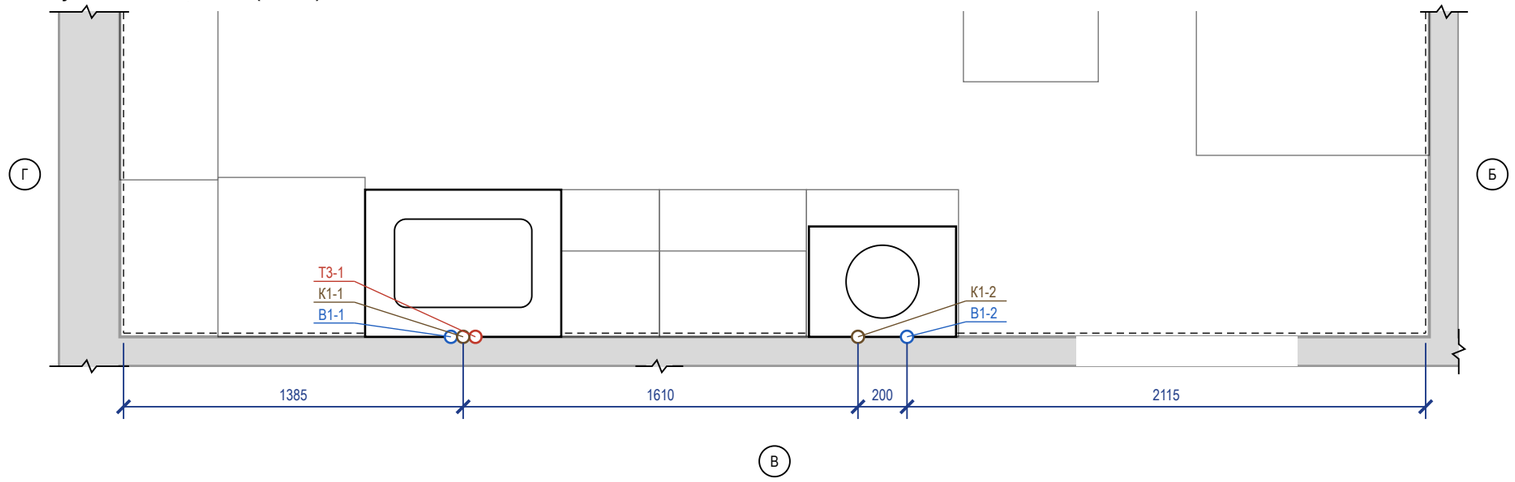

Фрагмент 2. Ванная, пом. 3 (М 1:25)

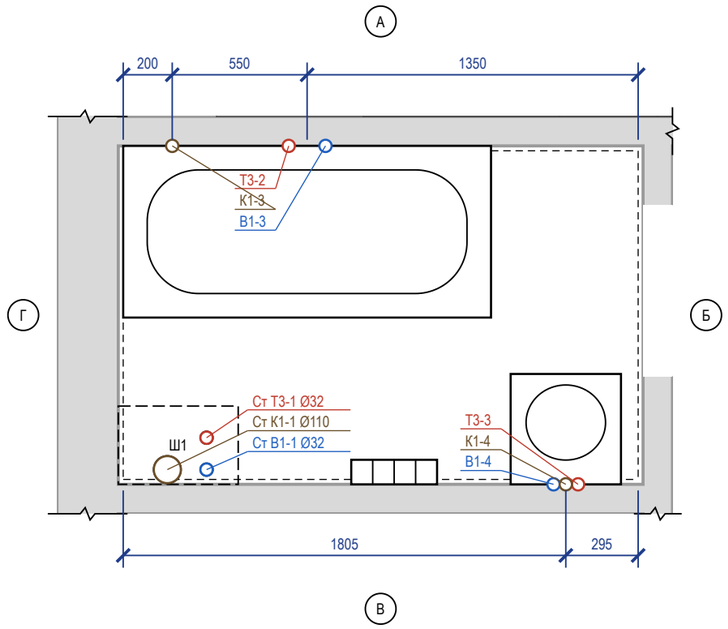

Фрагмент 3. Санузел, пом. 4 (М 1:25)

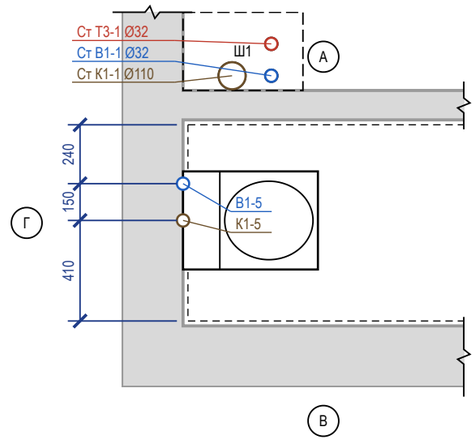

Ведомость привязок выводов

Код	Прибор	Ø	H, мм	Привязка от чист. стен, мм	Прим.
В1-1	С-01 мойка кухонная	½"	550	ст. В: 1335 от Г	межос. 100
Т3-1	—"	½"	550	ст. В: 1435 от Г	межос. 100
К1-1	—"	Ø50	400	ст. В: 1385 от Г	
В1-2	ОБ-02 стиральная машина	½"	600	ст. В: 2115 от Б	кран машины
К1-2	—"	Ø40	600	ст. В: 2315 от Б	
В1-3	С-02 ванна	½"	800	ст. А: 825 от Г	межос. 150
Т3-2	—"	½"	800	ст. А: 675 от Г	межос. 150
К1-3	—"	Ø50	50	ст. А: 200 от Г	
В1-4	С-03 умывальник	½"	550	ст. В: 345 от Б	межос. 100
Т3-3	—"	½"	550	ст. В: 245 от Б	межос. 100
К1-4	—"	Ø50	500	ст. В: 295 от Б	
В1-5	С-05 унитаз подвесной	½"	150	ст. Г: 240 от А	в раме инсталляции
К1-5	—"	Ø110	230	ст. Г: 390 от А	

Условные обозначения

- вывод В1 (код — в ведомости привязок)
- вывод Т3 (код — в ведомости привязок)
- вывод К1 (код — в ведомости привязок)
- сантехприбор по расстановке (габарит модели)
- чистовая поверхность стены (от неё привязки)
- стояк «Ст К1-N / Ст В1-N» (ГОСТ 21.601), Ø мм
- шахта / короб стояков, люк 300×400
- линия обрыва (граница фрагмента)
- А — обозначение стены А–Г (как на развёртках)


Примечания

1. Привязки выводов даны от чистовых поверхностей стен (облицовка на сторону: кухня-гостиная — 15 мм (по данным); ванная — 20 мм (по данным); санузел — 20 мм (по данным)); эти же грани — на развёртках и в раскладке плитки. Высоты — от чистого пола помещения.
2. До черновой разводки сверить по паспорту выбранного прибора (смеситель, инсталляция, сифон).
3. Горячая вода (Т3) — слева от холодной (В1), если смотреть на прибор. Допуск установки выводов: ±5 мм в группе, ±20 мм у отдельно стоящих.
4. Расчёт систем водоснабжения и канализации и подбор оборудования выполняет проектная организация; лист задаёт места и высоты выводов.
5. Стояки в коробах/шахтах Ш1 не замоноличивать; стояк К1 в коробе — звукоизоляция стояка в коробе без жёсткого контакта с трубой; к арматуре и ревизиям — люк не меньше 300×400.


	Лист	№ док.	Подпись	Дата	Проект: Квартира 58 м²	М 1:25
Дизайнер	Кырлан А.С.			14.11.26		
Проверил					План выводов сантехники	Стадия: П; Лист: 25; Листов: 92
Н. контр.						
Утв.						

выпуск 14.11.2026 № 2b6bd7c078 · стр. 25 из 92


План квартиры (М 1:200)

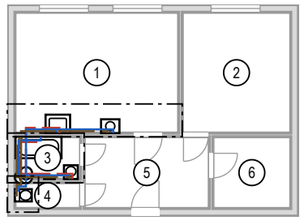


Фр. 1. Кухня-гостиная (М 1:25)

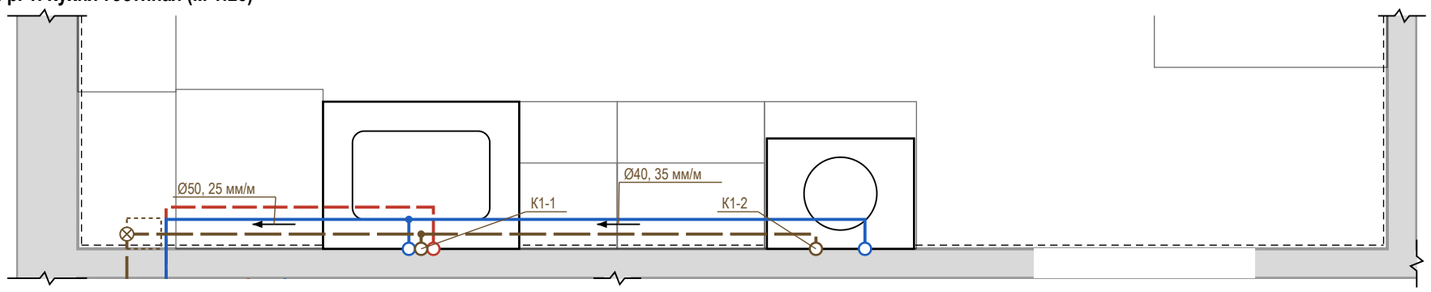

Фр. 2. Ванная (М 1:25)

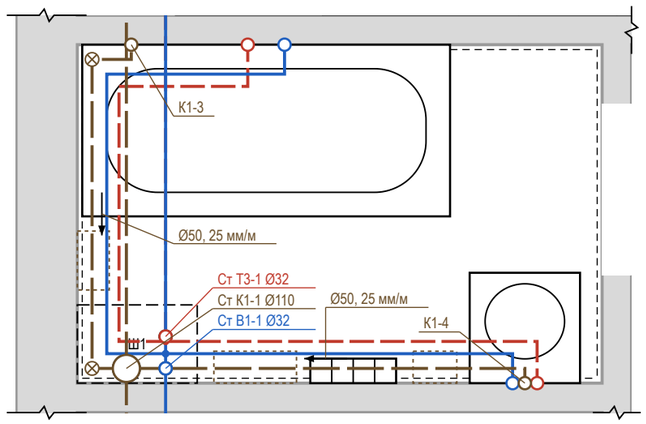

Фр. 3. Санузел (М 1:25)

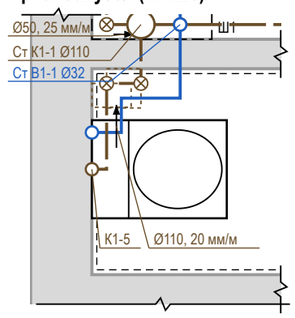

Условные обозначения

- В1 — водопровод хозяйственно-питьевой (ХВС), PP-R Ø20
- Т3 — горячее водоснабжение, подача (ГВС), PP-R Ø20
- К1 — канализация бытовая
- направление уклона К1 / пола: Ø, мм на 1 м
- ревизия (прочистка) К1 — доступ сохранить
- тройник (ответвление к прибору)
- короб К1 над чистым полом (ГКЛВ под плитку)
- вывод В1 (код — в ведомости привязок)
- вывод Т3 (код — в ведомости привязок)
- вывод К1 (код — в ведомости привязок)
- сантехприбор по расстановке (габарит модели)
- стояк «Ст К1-N / Ст В1-N» (ГОСТ 21.601), Ø мм
- шахта / короб стояков, люк 300×400
- линия обрыва (граница фрагмента)
- граница фрагмента на плане (Фр. N)

Профиль выпусков К1 (до врезки в стояк)

Выпуск	Прибор	Ø	L, м	i, мм/м	Δh, мм	Прокладка, мм
К1-5	С-05 унитаз подвесной	Ø110	0,79	20	16	короб 160×140
К1-1	С-01 мойка кухонная	Ø50	2,76	25	69	короб 150×110
К1-4	С-03 умывальник	Ø50	1,69	25	42	короб 130×110
К1-3	С-02 ванна	Ø50	1,62	25	41	короб 130×110
К1-2	ОБ-02 стиральная машина	Ø40	4,37	35	153	короб 230×110

Короб h×b: h — от чистого пола, b — от чистовой стены. Стяжка 90 мм — лист полов.

Узел ввода В1, Т3 (схема, без масштаба)



состав узла — по согласованию

⊗ Ст К1-1: ревизия на стояке — люк в коробе


Примечания

1. Трассы принципиальные, построены от стояков вдоль стен помещений; фактическое положение фиксируется исполнительной схемой с привязками (фото с рулеткой) до закрытия.
2. Уклон К1 не менее 1/d и не более 150 мм/м (СП 30.13330.2020, п. 19.1), приняты практические уклоны; поворот — двумя отводами 45°, ревизия после поворота, доступ сохранить. Стояк К1 в коробе — звукоизоляция стояка в коробе, без жёсткого контакта короба с трубой.
3. Решение по К1: стяжка 90 мм не укрывает трубы (нужно Ø + Δh + 45 мм) — выпуски идут над чистым полом вдоль стен; К1-5, К1-1, К1-4, К1-3, К1-2 — в коробе ГКЛВ под плитку (размеры в профиле). Короба — на развёртках; отметку низа врезки в стояк замерить до черновых работ.
4. Отводы К1-2 (4,4 м) длиннее 4 м без вентиляции — у прибора воздушный клапан Ø50 в доступном месте (за люком или в тумбе) либо вентилируемый отвод (EN 12056-2, табл. 4), подбор — проектная организация.
5. Состав узла ввода В1, Т3 — по согласованию: на схеме типовой узел — кран шаровой, фильтр, счётчик, обратный клапан, кран; состав и места не определены (записи реестра нет). Доступ к арматуре — через люк не меньше 300×400. Водопровод — в штробе стен или в коробах; трубы испытать давлением до закрытия (акт скрытых работ).
6. Расчёт систем, диаметры магистралей и подбор оборудования выполняет проектная организация; врезка и перенос стояков — по согласованию с управляющей организацией. Арматуру и привязки сверить по паспортам приборов.
7. Ведомость выводов (код, прибор, высота, привязка) — лист 25; на схеме — только коды.

	Лист	№ док.	Подпись	Дата	Проект: Квартира 58 м²			
Дизайнер	Кырлан А.С.			14.11.26	Схема разводки водопровода и канализации	Стадия	Лист	Листов
Проверил						П	26	92
Н. контр.								
Утв.								

выпуск 14.11.2026 № 2b6bd7c078 · стр. 26 из 92

Схема В1 (М 1:50)

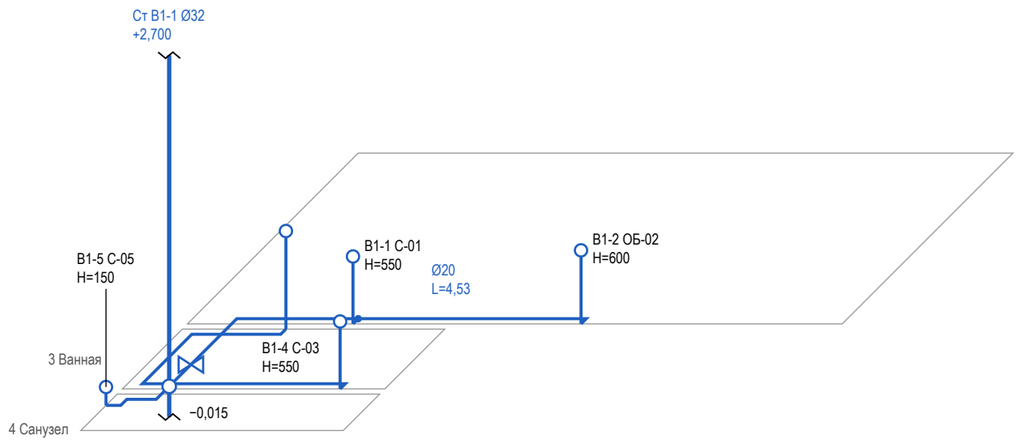

Ведомость выводов В1

Код	Прибор	H, мм	Ø, мм	Трасса, м
В1-2	ОБ-02 стиральная машина	600	20	4,53
В1-1	С-01 мойка кухонная	550	20	0,12
В1-3	С-02 ванна	800	20	2,23
В1-4	С-03 умывальник	550	20	1,53
В1-5	С-05 унитаз подвесной	150	20	0,80

Условные обозначения

- В1 — водопровод хозяйственно-питьевой (ХВС), PP-R Ø20
- вывод В1 (код — в ведомости привязок)
- стояк «Ст К1-N / Ст В1-N» (ГОСТ 21.601), Ø мм
- стояк в плане (на отметке пола); вертикаль — стояк по высоте, разрыв — перекрытие
- тройник (ответвление к прибору)
- кран шаровой

Примечания

1. Схема В1 построена по тем же трассам, что план разводки: положение в плане сохранено, глубина — в масштабе ×0,5. Трассы принципиальные; фактическое положение фиксируется исполнительной схемой до закрытия.
2. Высоты H — от чистого пола помещения, мм. Отметка прокладки магистрали В1 (в стяжке, в стене или по полу) в данных не задана: участки показаны на уровне пола условно (записи реестра нет).
3. Узел ввода В1 (кран, фильтр, счётчик, обратный клапан, кран) — на схеме разводки; состав узла ввода — по согласованию. Кран шаровой — на первом участке от стояка.
4. Трубы испытать давлением до закрытия (акт скрытых работ, опрессовка по СП 73.13330.2016).
5. Диаметры, высоты выводов и места кранов — по паспортам выбранных приборов и расчёту проектной организации.
6. Расчёт систем, диаметры магистралей и подбор оборудования выполняет проектная организация.

	Лист	№ док.	Подпись	Дата
Дизайнер	Кырлан А.С.			14.11.26
Проверил				
Н. контр.				
Утв.				


Проект: Квартира 58 м² — **М 1:50**

Аксонометрическая схема В1 (холодное водоснабжение)

Стадия	Лист	Листов
П	27	92

выпуск 14.11.2026 № 2b6bd7c078 · стр. 27 из 92

Схема Т3 (М 1:50)

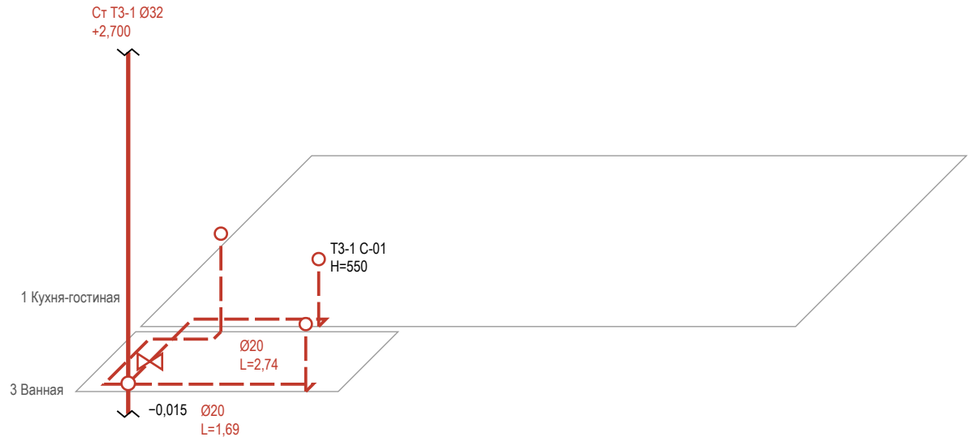

Ведомость выводов Т3

Код	Прибор	H, мм	Ø, мм	Трасса, м
Т3-1	С-01 мойка кухонная	550	20	2,74
Т3-2	С-02 ванна	800	20	1,95
Т3-3	С-03 умывальник	550	20	1,69

Условные обозначения

- Т3 — горячее водоснабжение, подача (ГВС), PP-R Ø20
- вывод Т3 (код — в ведомости привязок)
- стояк «Ст К1-N / Ст В1-N» (ГОСТ 21.601), Ø мм
- стояк в плане (на отметке пола); вертикаль — стояк по высоте, разрыв — перекрытие
- тройник (ответвление к прибору)
- кран шаровой


Примечания

1. Схема Т3 построена по тем же трассам, что план разводки: положение в плане сохранено, глубина — в масштабе ×0,5. Трассы принципиальные; фактическое положение фиксируется исполнительной схемой до закрытия.
2. Высоты H — от чистого пола помещения, мм. Отметка прокладки магистрали Т3 (в стяжке, в стене или по полу) в данных не задана: участки показаны на уровне пола условно (записи реестра нет).
3. Узел ввода Т3 (кран, фильтр, счётчик, обратный клапан, кран) — на схеме разводки; состав узла ввода — по согласованию. Кран шаровой — на первом участке от стояка.
4. Циркуляция ГВС в данных не задана — циркуляционного трубопровода на схеме нет (записи реестра нет).
5. Трубы испытать давлением до закрытия (акт скрытых работ, опрессовка по СП 73.13330.2016).
6. Диаметры, высоты выводов и места кранов — по паспортам выбранных приборов и расчёту проектной организации.
7. Расчёт систем, диаметры магистралей и подбор оборудования выполняет проектная организация.

	Лист	№ док.	Подпись	Дата	Проект: Квартира 58 м²			М 1:50
Дизайнер	Кырлан А.С.			14.11.26	Аксонометрическая схема Т3 (горячее водоснабжение)	Стадия	Лист	Листов
Проверил						П	28	92
Н. контр.								
Утв.								

выпуск 14.11.2026 № 2b6bd7c078 · стр. 28 из 92

Схема К1 (М 1:50)

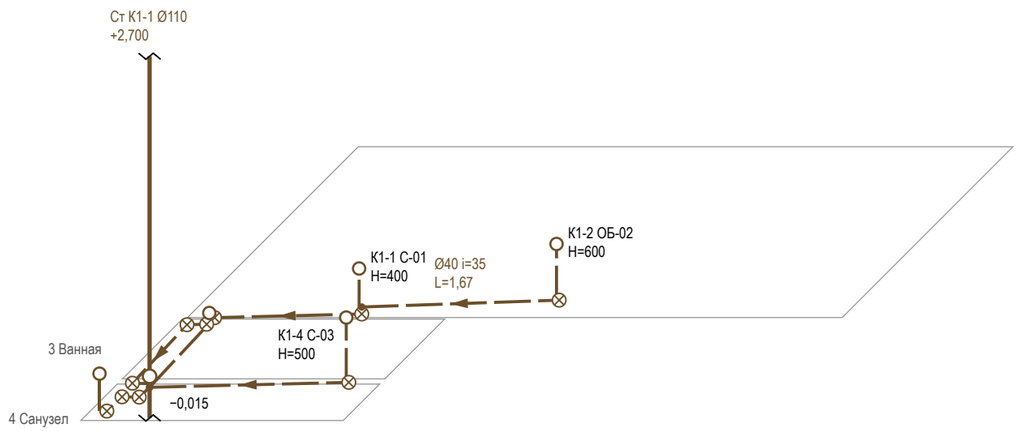

Ведомость выводов К1

Код	Прибор	H, мм	Ø, i	Трасса, м
К1-5	С-05 унитаз подвесной	230	110 i=20	0,79
К1-1	С-01 мойка кухонная	400	50 i=25	2,76
К1-4	С-03 умывальник	500	50 i=25	1,69
К1-3	С-02 ванна	50	50 i=25	1,62
К1-2	ОБ-02 стиральная машина	600	40 i=35	1,67

Условные обозначения

- К1 — канализация бытовая
- вывод К1 (код — в ведомости привязок)
- стояк «Ст К1-N / Ст В1-N» (ГОСТ 21.601), Ø мм
- стояк в плане (на отметке пола); вертикаль — стояк по высоте, разрыв — перекрытие
- направление уклона К1 / пола: Ø, мм на 1 м
- ревизия (прочистка) К1 — доступ сохранить
- тройник (ответвление к прибору)


Примечания

1. Схема К1 построена по тем же трассам, что план разводки: положение в плане сохранено, глубина — в масштабе ×0,5. Трассы принципиальные; фактическое положение фиксируется исполнительной схемой до закрытия.
2. Отметки — от плиты перекрытия: низ трубы у врезки в стояк — отметка из данных выпуска, к прибору труба поднимается на уклон i, мм/м (уклон не менее 1/d и не более 150 мм/м, СП 30.13330.2020, п. 19.1); чистый пол — выше плиты на стяжку (высота пирога пола). Высота выпуска прибора H — от чистого пола.
3. Ревизия — на повороте и в начале участка; стояк К1 в коробе с люком — звукоизоляция стояка в коробе; поворот — двумя отводами 45°.
4. Трубы испытать давлением до закрытия (акт скрытых работ, опрессовка по СП 73.13330.2016).
5. Диаметры, высоты выводов и места кранов — по паспортам выбранных приборов и расчёту проектной организации.
6. Расчёт систем, диаметры магистралей и подбор оборудования выполняет проектная организация.

	Лист	№ док.	Подпись	Дата	Проект: Квартира 58 м²			М 1:50
Дизайнер	Кырлан А.С.			14.11.26	Аксонометрическая схема К1 (канализация)	Стадия	Лист	Листов
Проверил						П	29	92
Н. контр.								
Утв.								

выпуск 14.11.2026 № 2b6bd7c078 · стр. 29 из 92

Стена В (М 1:20)

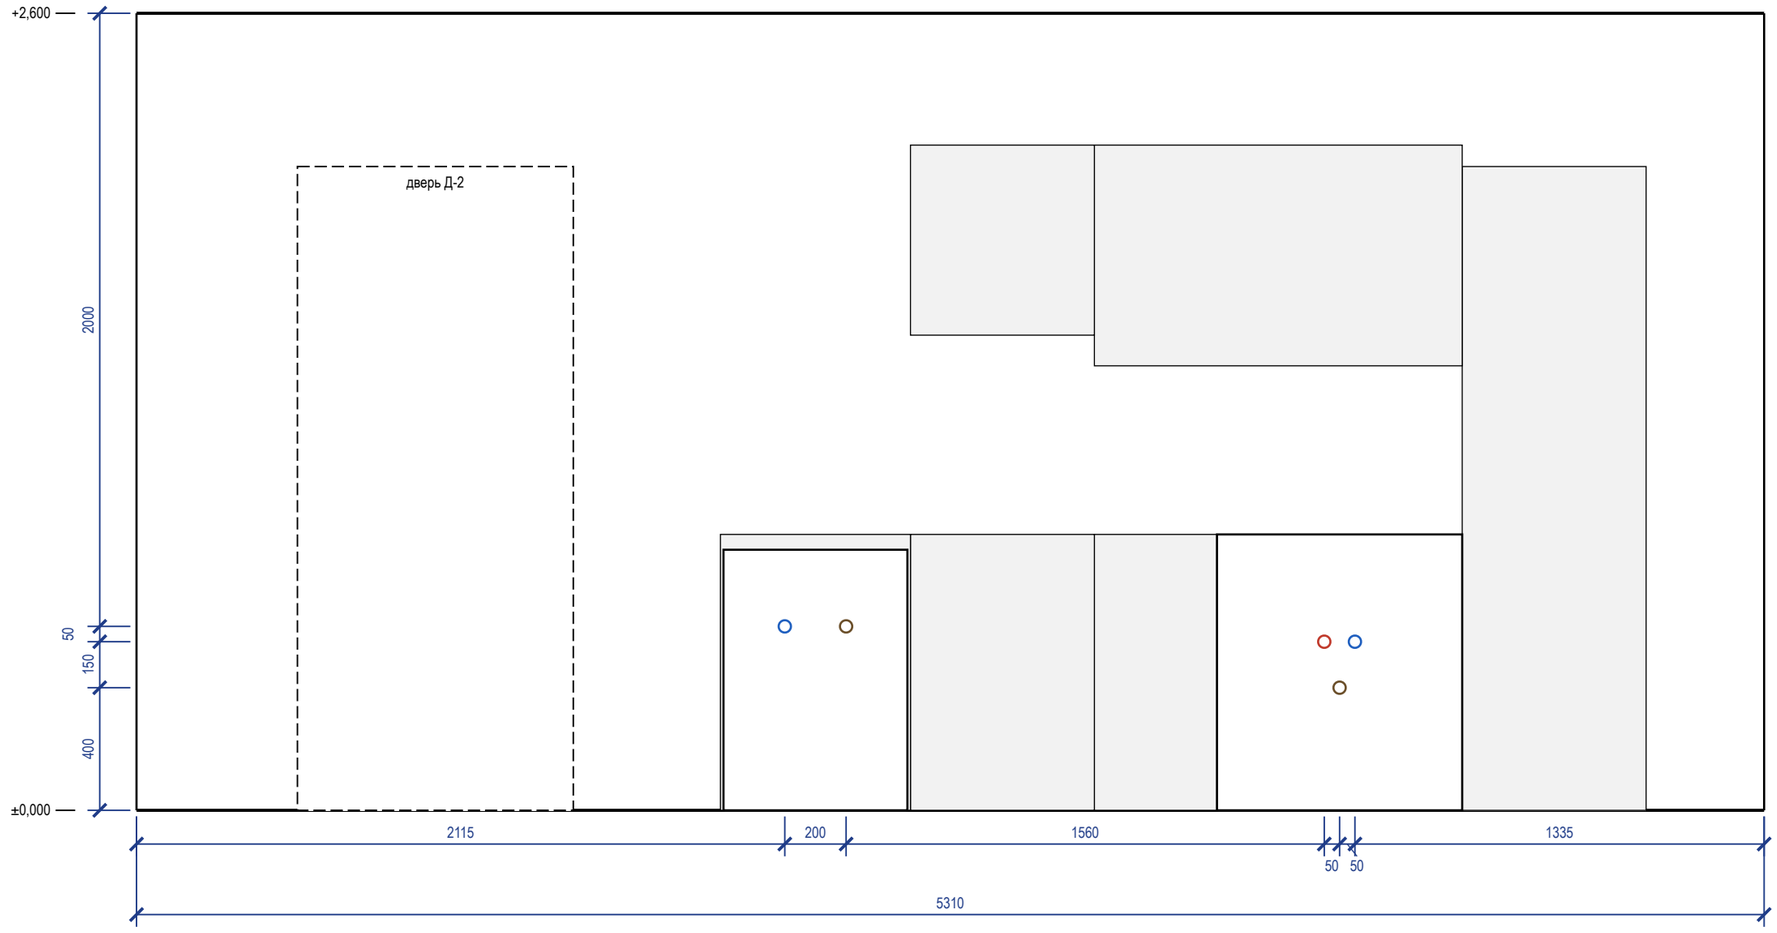

Ведомость привязок выводов (от чистого пола и угла)

Код	Прибор	Ø	H, мм	Привязка, мм
В1-1	С-01 мойка кухонная	½"	550	ст. В: 3975 от лев. угла
Т3-1	С-01 мойка кухонная	½"	550	ст. В: 3875 от лев. угла
К1-1	С-01 мойка кухонная	Ø50	400	ст. В: 3925 от лев. угла
В1-2	ОБ-02 стиральная машина	½"	600	ст. В: 2115 от лев. угла
К1-2	ОБ-02 стиральная машина	Ø40	600	ст. В: 2315 от лев. угла

Условные обозначения

- вывод В1 (код — в ведомости привязок)
- вывод Т3 (код — в ведомости привязок)
- вывод К1 (код — в ведомости привязок)
- сантехприбор по расстановке (габарит модели)
- дверной проём; окно — сплошной контур


Примечания

1. Габариты и высоты приборов, межосевые смесителей и места кранов — по паспортам выбранных приборов, сверяются до разметки стен.
2. Высоты H — от чистого пола помещения, мм; отметка чистого пола и потолка — у левого края вида (от ±0,000 объекта). Привязки — от левого чистового угла вида (облицовка стен вычтена), как на развёртках стен.
3. Ревизионные люки к арматуре и ревизиям в данных не заданы: место и размер не определены (записи реестра нет).
4. Мойка, ПММ и фильтр — выводы в шкафу мойки; диаметры и положение сифона и кранов сверить по паспортам приборов и чертежам модуля.
5. Часть подписей выводов не уместилась у знака: коды и высоты — в ведомости привязок.
6. Расчёт систем водоснабжения и канализации и подбор оборудования выполняет проектная организация; лист задаёт места и высоты выводов.


	Лист	№ док.	Подпись	Дата	Проект: Квартира 58 м²			М 1:20
Дизайнер	Кырлан А.С.			14.11.26	Развёртки мокрых зон: выводы ВК. Кухня-гостиная	Стадия	Лист	Листов
Проверил						П	30	92
Н. контр.								
Утв.								

выпуск 14.11.2026 № 2b6bd7c078 · стр. 30 из 92


Стена А (М 1:25)

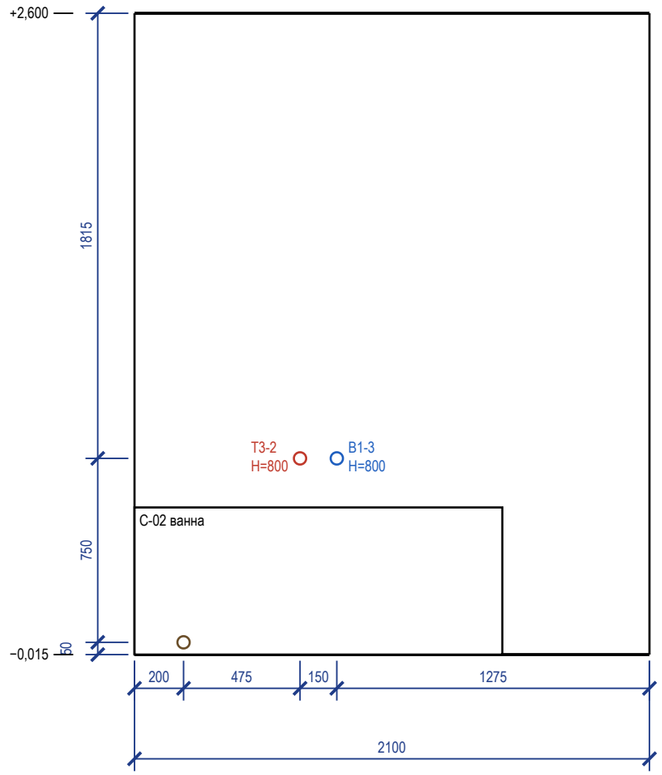


Стена Б (М 1:25)

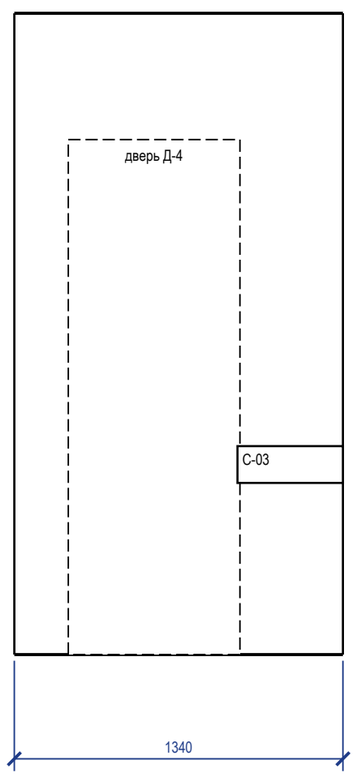

Стена В (М 1:25)

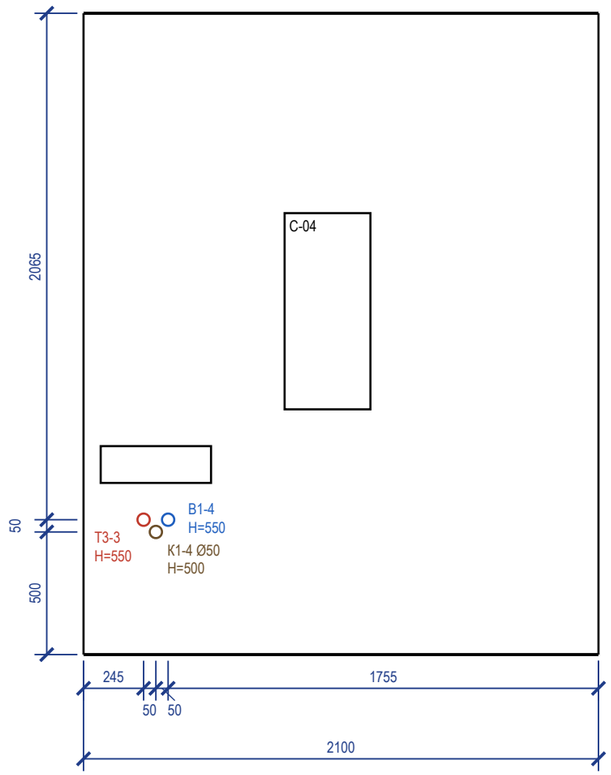

Стена Г (М 1:25)

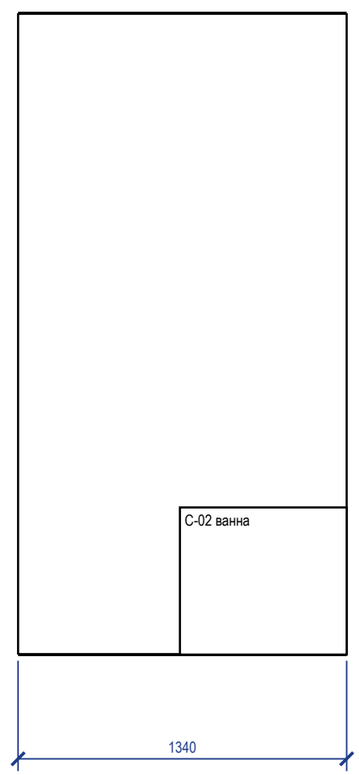

Ведомость привязок выводов (от чистого пола и угла)

Код	Прибор	Ø	H, мм	Привязка, мм
В1-3	С-02 ванна	½"	800	ст. А: 825 от лев. угла
Т3-2	С-02 ванна	½"	800	ст. А: 675 от лев. угла
К1-3	С-02 ванна	Ø50	50	ст. А: 200 от лев. угла
В1-4	С-03 умывальник	½"	550	ст. В: 345 от лев. угла
Т3-3	С-03 умывальник	½"	550	ст. В: 245 от лев. угла
К1-4	С-03 умывальник	Ø50	500	ст. В: 295 от лев. угла

Условные обозначения

- вывод В1 (код — в ведомости привязок)
- вывод Т3 (код — в ведомости привязок)
- вывод К1 (код — в ведомости привязок)
- сантехприбор по расстановке (габарит модели)
- дверной проём; окно — сплошной контур


Примечания

1. Габариты и высоты приборов, межосевые смесителей и места кранов — по паспортам выбранных приборов, сверяются до разметки стен.
2. Высоты Н — от чистого пола помещения, мм; отметка чистого пола и потолка — у левого края вида (от ±0,000 объекта). Привязки — от левого чистового угла вида (облицовка стен вычтена), как на развёртках стен.
3. Стояки в помещении: Ст К1-1 Ø110, Ст В1-1 Ø32, Ст Т3-1 Ø32 — положение на плане выводов; выводы подключаются к ним по схеме разводки.
4. Ревизионные люки к арматуре и ревизиям в данных не заданы: место и размер не определены (записи реестра нет).
5. Часть подписей выводов не уместилась у знака: коды и высоты — в ведомости привязок.
6. Расчёт систем водоснабжения и канализации и подбор оборудования выполняет проектная организация; лист задаёт места и высоты выводов.

	Лист	№ док.	Подпись	Дата	Проект: Квартира 58 м²	М 1:25		
Дизайнер	Кырлан А.С.			14.11.26	Развёртки мокрых зон: выводы ВК. Ванная	Стадия	Лист	Листов
Проверил						П	31	92
Н. контр.								
Утв.								

выпуск 14.11.2026 № 2b6bd7c078 · стр. 31 из 92

Стена Г (М 1:20)

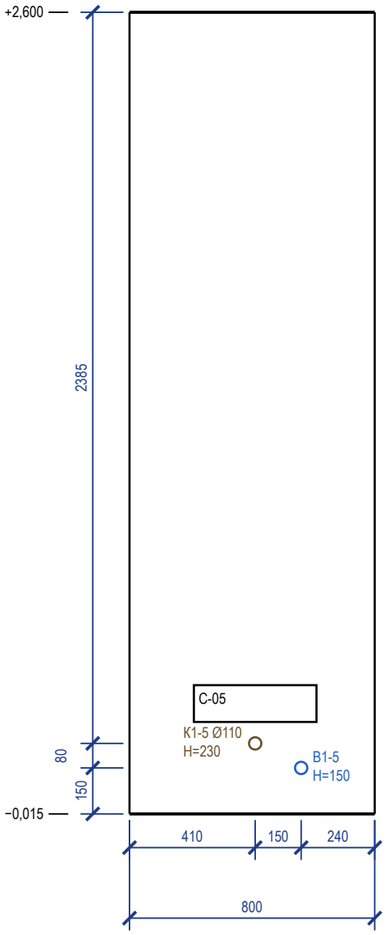

Ведомость привязок выводов (от чистого пола и угла)

Код	Прибор	Ø	H, мм	Привязка, мм
B1-5	C-05 унитаз подвесной	½"	150	ст. Г: 560 от лев. угла
K1-5	C-05 унитаз подвесной	Ø110	230	ст. Г: 410 от лев. угла

Условные обозначения

- вывод B1 (код — в ведомости привязок)
- вывод T3 (код — в ведомости привязок)
- вывод K1 (код — в ведомости привязок)
- сантехприбор по расстановке (габарит модели)
- дверной проём; окно — сплошной контур

Примечания

1. Габариты и высоты приборов, межосевые смесителей и места кранов — по паспортам выбранных приборов, сверяются до разметки стен.
2. Высоты H — от чистого пола помещения, мм; отметка чистого пола и потолка — у левого края вида (от ±0,000 объекта). Привязки — от левого чистового угла вида (облицовка стен вычтена), как на развёртках стен.
3. Ревизионные люки к арматуре и ревизиям в данных не заданы: место и размер не определены (записи реестра нет).
4. Расчёт систем водоснабжения и канализации и подбор оборудования выполняет проектная организация; лист задаёт места и высоты выводов.

	Лист	№ док.	Подпись	Дата
Дизайнер	Кырлан А.С.			14.11.26
Проверил				
Н. контр.				
Утв.				

Проект: Квартира 58 м² — **М 1:20**

Развёртки мокрых зон: выводы ВК. Санузел

Стадия	Лист	Листов
П	32	92

выпуск 14.11.2026 № 2b6bd7c078 · стр. 32 из 92


Поз.	Наименование и техническая характеристика	Тип, марка, обозначение документа	Код продукции	Поставщик	Ед. изм.	Кол.	Масса 1 ед., кг	Примечание
	Санитарные приборы							
1	Ванна встраиваемая акриловая 1500×700 мм, с каркасом, экраном и отверстием слив-перелив	акриловая 1500×700, смеситель настенный		выбор заказчика	шт	1		С-02
2	Унитаз подвесной безободковый, с сиденьем микролифт, крепёж и звукоизолирующая прокладка	Laufen Pro 8.2096.6.000.000.1		выбор заказчика	шт	1		С-05
3	Инсталляция для подвесного унитаза: рама высотой 1120 мм, бачок, клавиша смыва (ось клавиши 1050 мм от чистого пола)	аналог		выбор заказчика	шт	1		С-05; короб ГКЛВ
4	Умывальник подвесной 450×450 мм, с отверстием под смеситель и переливом	Laufen Pro S 8.1096.3.000.104.1		выбор заказчика	шт	1		С-03
5	Мойка кухонная 700×480 мм, с переливом	мойка врезная 700×480 в шкафу М-02		с кухонной мебелью	шт	1		С-01
6	Полотенцесушитель электрический, IP44, с терморегулятором	аналог		выбор заказчика	шт	1		С-04
	Смесители, сифоны и арматура приборов							
7	Смеситель для ванны настенный однорычажный, межосевое 150 мм, с душевым набором (лейка, шланг, держатель)	аналог		выбор заказчика	шт	1		С-02
8	Смеситель для умывальника однорычажный, с донным клапаном	аналог		выбор заказчика	шт	1		С-03
9	Смеситель кухонный однорычажный, высокий излив	аналог		выбор заказчика	шт	1		С-01
10	Обвязка ванны слив-перелив Ø40/50 с сифоном	аналог		выбор заказчика	шт	1		С-02
11	Сифон для умывальника бутылочный Ø32/40–50, с гофрой к выпуску	аналог		выбор заказчика	шт	1		С-03
12	Сифон для мойки Ø40/50	аналог		выбор заказчика	шт	1		С-01
13	Сифон для стиральной машины встраиваемый в стену Ø50, с обратным клапаном	аналог		выбор заказчика	шт	1		ОБ-02
14	Кран угловой ½"×½" с гибкой подводкой 40 см (умывальники, мойка)	аналог		выбор заказчика	шт	4		по 2 на прибор
15	Кран шаровой угловой ½"×¾" для подключения стиральной и посудомоечной машины	аналог		выбор заказчика	шт	1		ОБ-02
	Трубопроводы							
16	Труба полипропиленовая PP-R PN20 Ø20×3,4 (В1)	ГОСТ 32415-2013		выбор заказчика	м	13,5	0,17	9,2 + 2,6 + 10 %
17	Труба PP-R, армированная стекловолокном, PN20 Ø20×2,8 (Т3)	ГОСТ 32415-2013		выбор заказчика	м	9,5	0,15	6,4 + 1,9 + 10 %
18	Труба канализационная ПП Ø40 (К1)	ГОСТ 32414-2013		выбор заказчика	м	2,5		1,7 + 0,6 + 10 %
19	Труба канализационная ПП Ø50 (К1)	ГОСТ 32414-2013		выбор заказчика	м	8		6,1 + 0,9 + 10 %
20	Труба канализационная ПП Ø110 (К1)	ГОСТ 32414-2013		выбор заказчика	м	1,5		0,8 + 0,2 + 10 %
	Фасонные части и выводы							
21	Отвод канализационный ПП 45° Ø40	ГОСТ 32414-2013		выбор заказчика	шт	2		2 шт. на поворот
22	Отвод канализационный ПП 45° Ø50	ГОСТ 32414-2013		выбор заказчика	шт	12		2 шт. на поворот
23	Отвод канализационный ПП 45° Ø110	ГОСТ 32414-2013		выбор заказчика	шт	6		2 шт. на поворот
24	Тройник канализационный ПП 45° (врезки ветвей)	ГОСТ 32414-2013		выбор заказчика	шт	4		
25	Ревизия канализационная ПП (после поворота трассы)	ГОСТ 32414-2013		выбор заказчика	шт	5		доступ сохранить
26	Фитинги PP-R Ø20: тройники, угольники 90° (ветви и повороты В1, Т3)	ГОСТ 32415-2013		выбор заказчика	шт	22		
27	Водорозетка PP-R Ø20×½" настенная, с креплением	ГОСТ 32415-2013		выбор заказчика	шт	8		коды — лист выводов
	Узлы ввода, люки, короба							
28	Кран шаровой латунный Ду15 PN16 (отключение ввода)	аналог		выбор заказчика	шт	2		Ст В1-1, Ст Т3-1
29	Фильтр сетчатый косой Ду15	аналог		выбор заказчика	шт	2		
30	Счётчик воды крыльчатый Ду15 (ХВ, ГВ), с поверкой	аналог		выбор заказчика	шт	2		пломба УК
31	Клапан обратный Ду15	аналог		выбор заказчика	шт	2		
32	Люк ревизионный нажимной под плитку 300×400 мм	аналог		выбор заказчика	шт	1		к стоякам и арматуре
33	Звукоизоляция стояка К1 в коробе: рулонный звукоизоляционный материал ≥ 10 мм, обмотка стояка на высоту этажа	аналог		выбор заказчика	м	2,7		Ст К1-1
34	Короб К1 над полом: профиль ПН/ПС, ГКЛВ 12,5 мм под плитку	аналог		выбор заказчика	м	1,6		сечение — лист разводки

Примечания

1. Форма 1 ГОСТ 21.110-2013, ширины граф изменены по п. 4.1. «Аналог» — аналог по характеристикам: модели внести до черновых работ, привязки выводов сверить по паспортам.
2. Бытовая техника не входит (показана арматура подключения), мойка — в комплекте кухни (марка — модуля кухни, как у столяра). Длины труб — трасса листа разводки + подъёмы + 10 %.
3. Стояк К1 в коробе — звукоизоляция стояка в коробе без жёсткого контакта короба с трубой.
4. Расчёт систем водоснабжения и канализации, диаметры магистралей и подбор оборудования выполняет проектная организация.

	Лист	№ док.	Подпись	Дата	Проект: Квартира 58 м²			
Дизайнер	Кырлан А.С.			14.11.26	Спецификация сантехнического оборудования	Стадия	Лист	Листов
Проверил						П	33	92
Н. контр.								
Утв.								

выпуск 14.11.2026 № 2b6bd7c078 · стр. 33 из 92

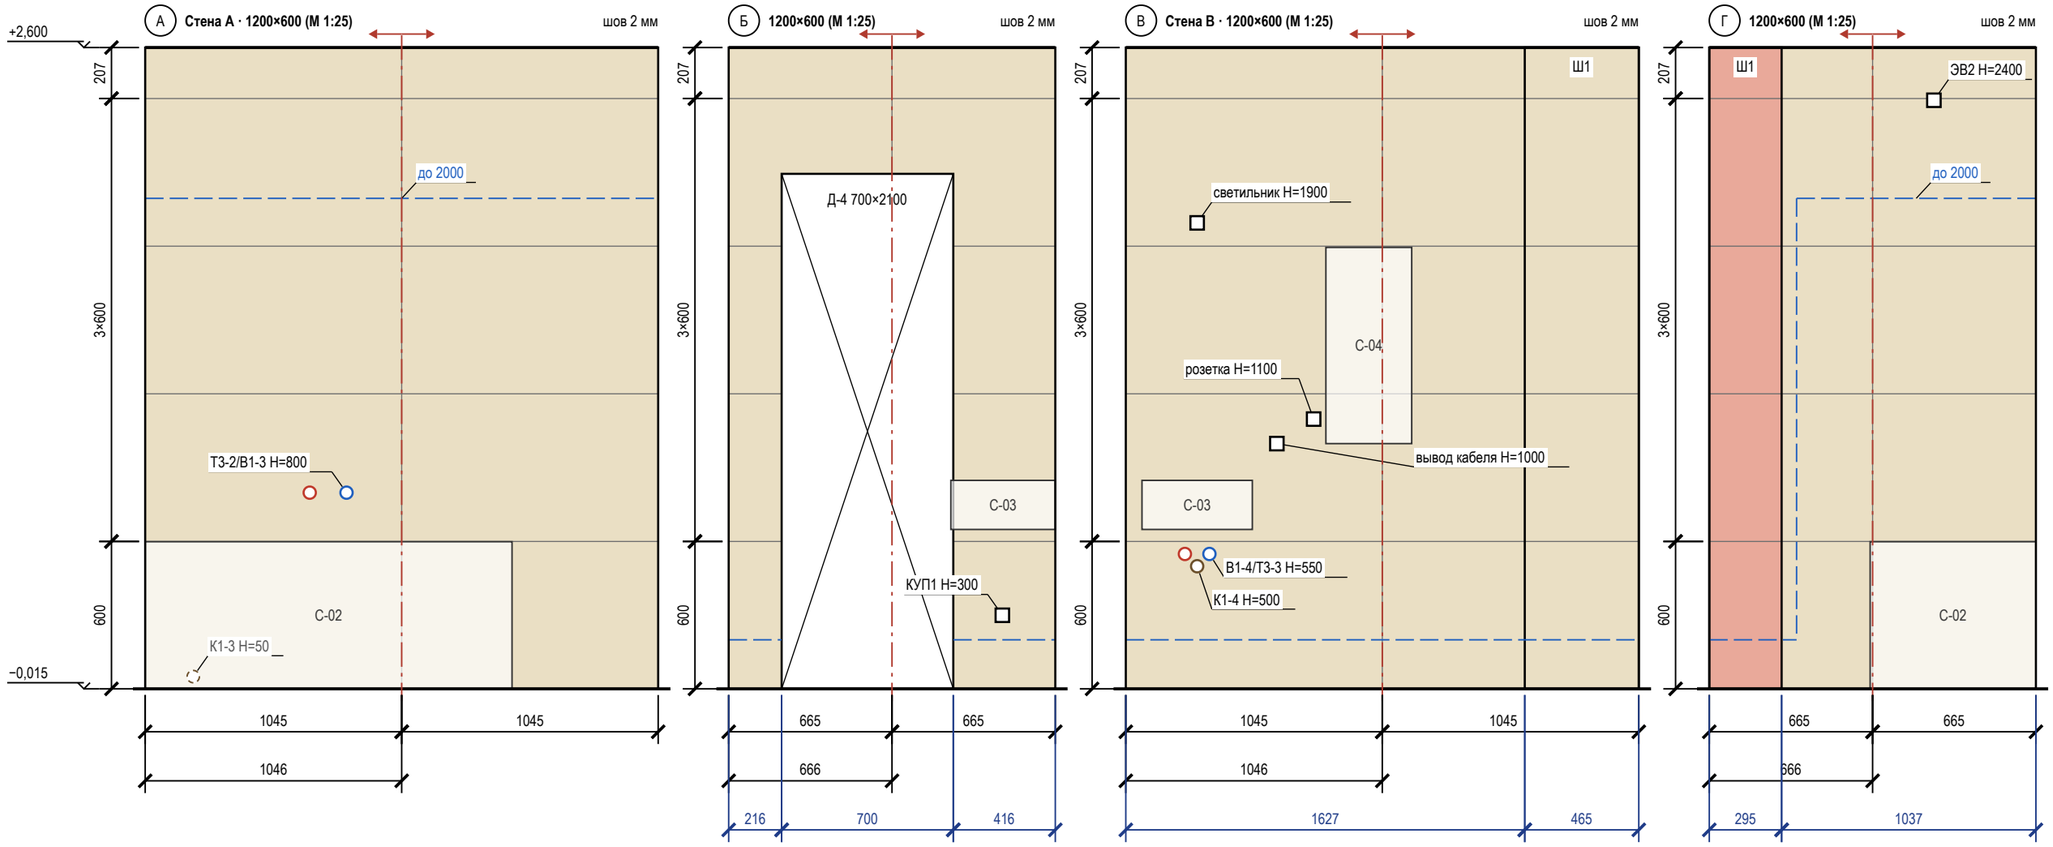

Подсчёт плитки по стенам и коробу

Поверхность	L × H, мм	S, м²	Целых	Подр.	С запасом	Подрезки: край / верх, мм
стена А	2092 × 2615	5,60	0	10	11	1045 / 1045; 207
стена Б	1332 × 2615	2,14	0	10	11	665 / 665; 207
стена В	2092 × 2615	4,38	0	10	11	1045 / 1045; 207
Ш1 489×319, ст. В	465 × 2615	1,22	0	5	6	лицо 465
стена Г	1332 × 2615	2,84	0	10	11	665 / 665; 207
Ш1 489×319, ст. Г	295 × 2615	0,77	0	5	6	лицо 295
Итого		**16,94**	**0**	**50**	**56**	

Сдвиг точек под раскладку

Точка (ВК, ЭОМ)	Стена	Проект: от угла / Н	Под раскладку: от угла / Н	Сдвиг, мм
розетка	В	766 / 1100	766 / 1203	Н +103
вывод кабеля	В	616 / 1000	616 / 902	Н −98
светильник	В	291 / 1900	291 / 1805	Н −95

Примечания

1. Вид изнутри, стены по часовой стрелке А → Г. Высоты — от чистого пола (−0,015), отметки — от ±0,000. Раскладка от чистовых размеров (штукатурка 10 + клей 5 + плитка 9 мм), подрезки чистые; старт — от оси стены, ряды от пола целыми.
2. Облицовка до потолка (+2,600).
3. Точки из таблицы сдвигов переносятся до черновой разводки (ЭОМ — по тем же числам).
4. Выводы ВК стоят по оси прибора и с прибором не двигаются — привязки по «Плану выводов сантехники» без сдвига; вне сетки (Т3-2/В1-3, В1-4/Т3-3, К1-4) отверстие в плитке коронкой по той же привязке, плитку не сдвигать.
5. За приборами и в коробе (К1-3) — штриховым кольцом.
6. Гидроизоляция: 200 мм от ЧП по периметру; над ванной — до 2000 и 300 мм за борт (СП 29.13330.2011, п. 7.2 — на высоту замачивания); углы — лентой; акт скрытых работ, пролив.
7. Короб стояков Ш1: грани 465 мм (ст. В), 295 мм (ст. Г) — плиткой стен по рядам стены, целая плитка от наружного угла; угол — запил 45° или профиль; за коробом плитку не кладут. Люк 300×400 — на грани ст. В: высота — по месту ревизии стояка (положение стояков сверяется на объекте), кромки дверцы по швам сетки, дверца нажимная под плитку.

Условные обозначения

- плитка целая; тонкая линия — шов
- плитка с подрезкой (размер — на цепочке)
- ось старта; стрелки — направление укладки
- верх гидроизоляции: 200 от ЧП, в мокрой зоне — «до …»
- проём — не облицовывается
- сантехприбор: габарит, высота по практике
- грань короба стояков (Ш…): своя сетка, за коробом плитку не кладут
- вывод В1 (код — в ведомости привязок)
- вывод Т3 (код — в ведомости привязок)
- вывод К1 (код — в ведомости привязок)
- вывод за прибором / в коробе (не на сетке)
- электроточка: марка и Н — по листам ЭОМ
- отметка уровня, м: ±0,000 — чистый пол жилых помещений
- низ потолка; серая полоса — стена без плитки
- А — обозначение стены А–Г (как на развёртках)


	Лист	№ док.	Подпись	Дата
Дизайнер	Кырлан А.С.			14.11.26
Проверил				
Н. контр.				
Утв.				

Проект: Квартира 58 м² — **М 1:25**

Раскладка плитки. Ванная. Развёртки стен

Стадия	Лист	Листов
П	34	92

выпуск 14.11.2026 № 2b6bd7c078 · стр. 34 из 92

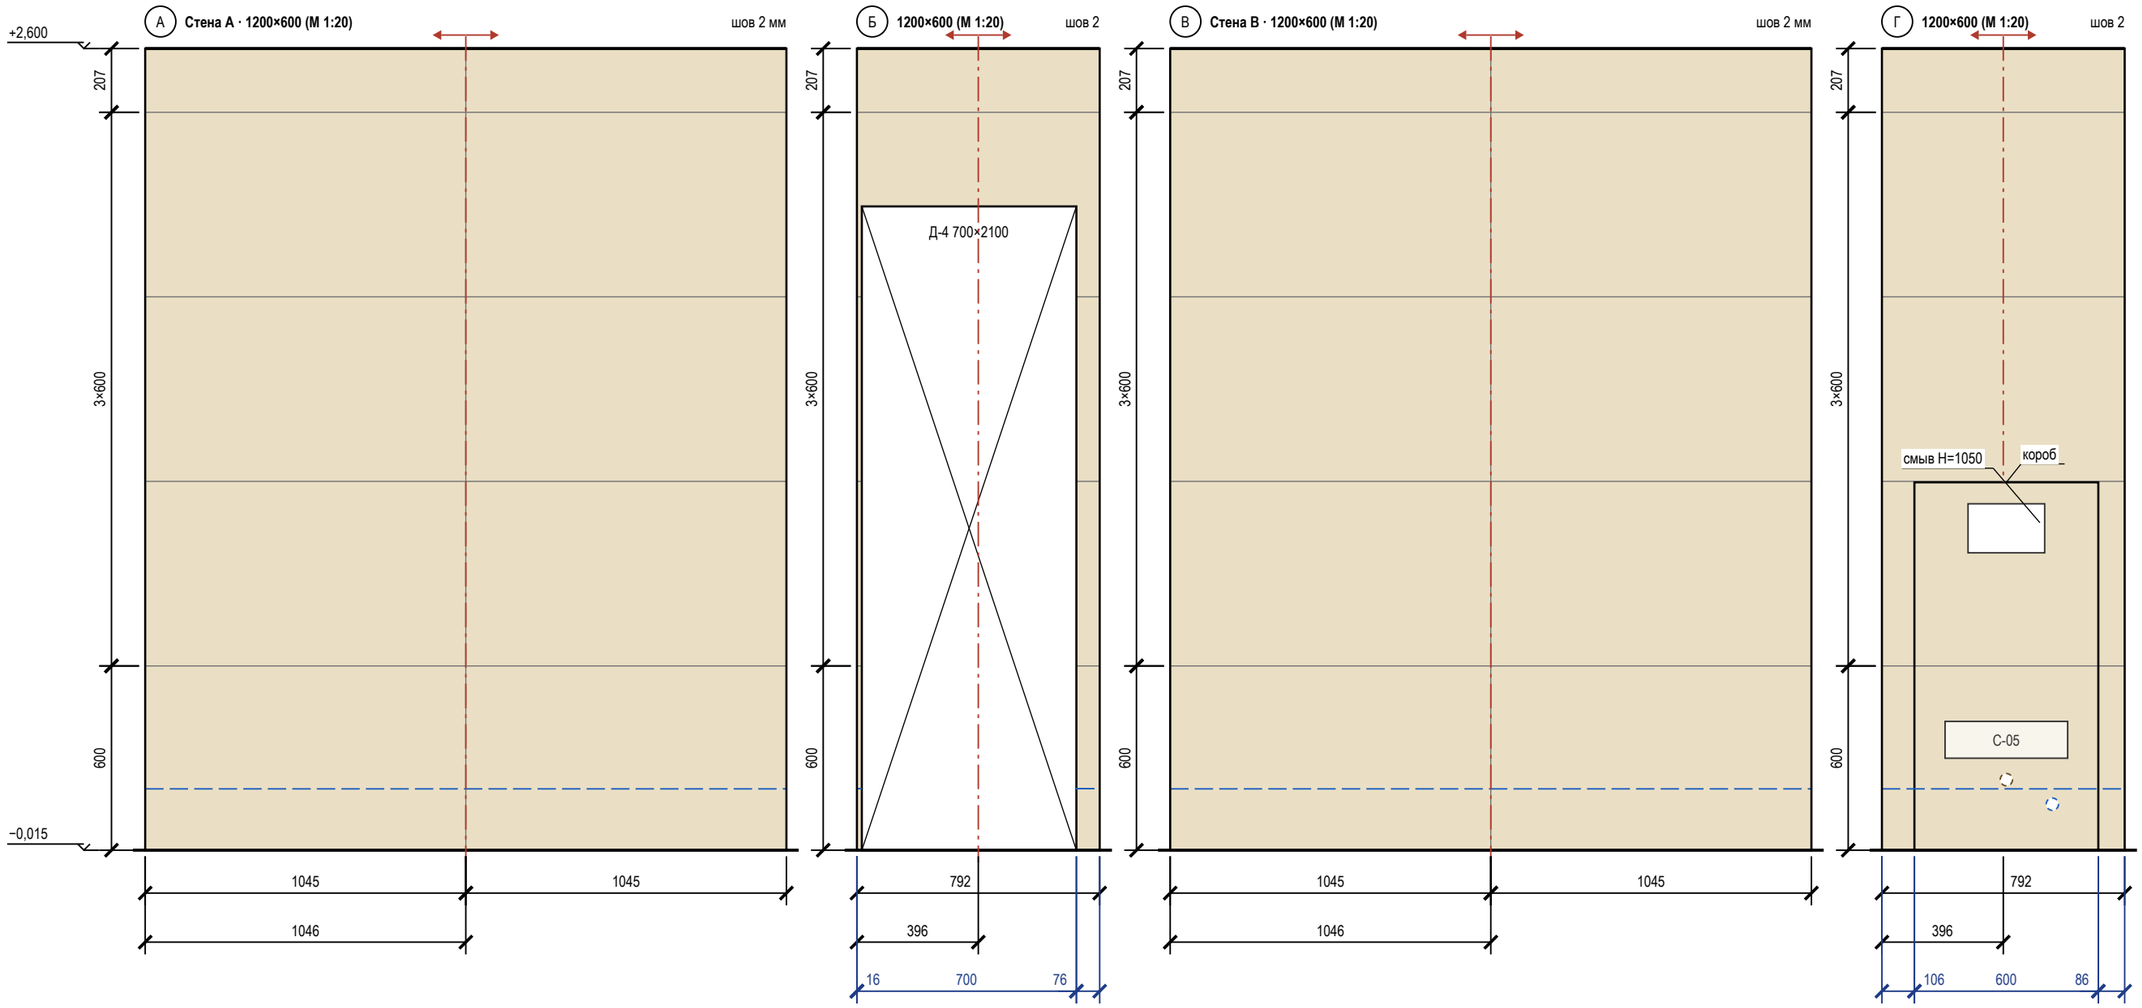

Подсчёт плитки по стенам и коробу

Поверхность	L × H, мм	S, м²	Целых	Подр.	С запасом	Подрезки: край / верх, мм
стена А	2092 × 2615	5,60	0	10	11	1045 / 1045; 207
стена Б	792 × 2615	0,73	0	5	6	792; 207
стена В	2092 × 2615	5,60	0	10	11	1045 / 1045; 207
стена Г	792 × 2615	1,48	0	5	6	792; 207
короб (ст. Г)	600×1200×250	1,47	0	7	8	лицо 600; бок. 250
Итого		**14,87**	**0**	**37**	**42**	

Условные обозначения

- плитка целая; тонкая линия — шов
- плитка с подрезкой (размер — на цепочке)
- ось старта; стрелки — направление укладки
- верх гидроизоляции: 200 от ЧП, в мокрой зоне — «до …»
- проём — не облицовывается
- сантехприбор: габарит, высота по практике
- короб инсталляции, в нём кнопка смыва 250×160
- вывод В1 (код — в ведомости привязок)
- вывод К1 (код — в ведомости привязок)
- вывод за прибором / в коробе (не на сетке)
- отметка уровня, м: ±0,000 — чистый пол жилых помещений
- низ потолка; серая полоса — стена без плитки
- обозначение стены А–Г (как на развёртках)

Примечания

1. Вид изнутри, стены по часовой стрелке А → Г. Высоты — от чистого пола (−0,015), отметки — от ±0,000. Раскладка от чистовых размеров (штукатурка 10 + клей 5 + плитка 9 мм), подрезки чистые; старт — от оси стены, ряды от пола целыми.
2. Облицовка до потолка (+2,600).
3. Открытые выводы и электроточки — на шве или в центре плитки (допуск 10 мм; плитка от 900 мм по высоте — на шве или не ближе 60 мм к нему).
4. За приборами и в коробе (В1-5, К1-5) — штриховым кольцом.
5. Гидроизоляция: 200 мм от ЧП по периметру; углы — лентой; акт скрытых работ, пролив.
6. Короб 600×1200×250: лицо 600 мм от оси кнопки смыва, боковины, полка; углы — запил 45° или профиль; за коробом плитку не кладут.
7. Между коробом и углом полоса 86 и 106 мм — довести короб до угла.


	Лист	№ док.	Подпись	Дата
Дизайнер	Кырлан А.С.			14.11.26
Проверил				
Н. контр.				
Утв.				

Проект: Квартира 58 м² — **М 1:20**

Раскладка плитки. Санузел. Развёртки стен

Стадия	Лист	Листов
П	35	92

выпуск 14.11.2026 № 2b6bd7c078 · стр. 35 из 92

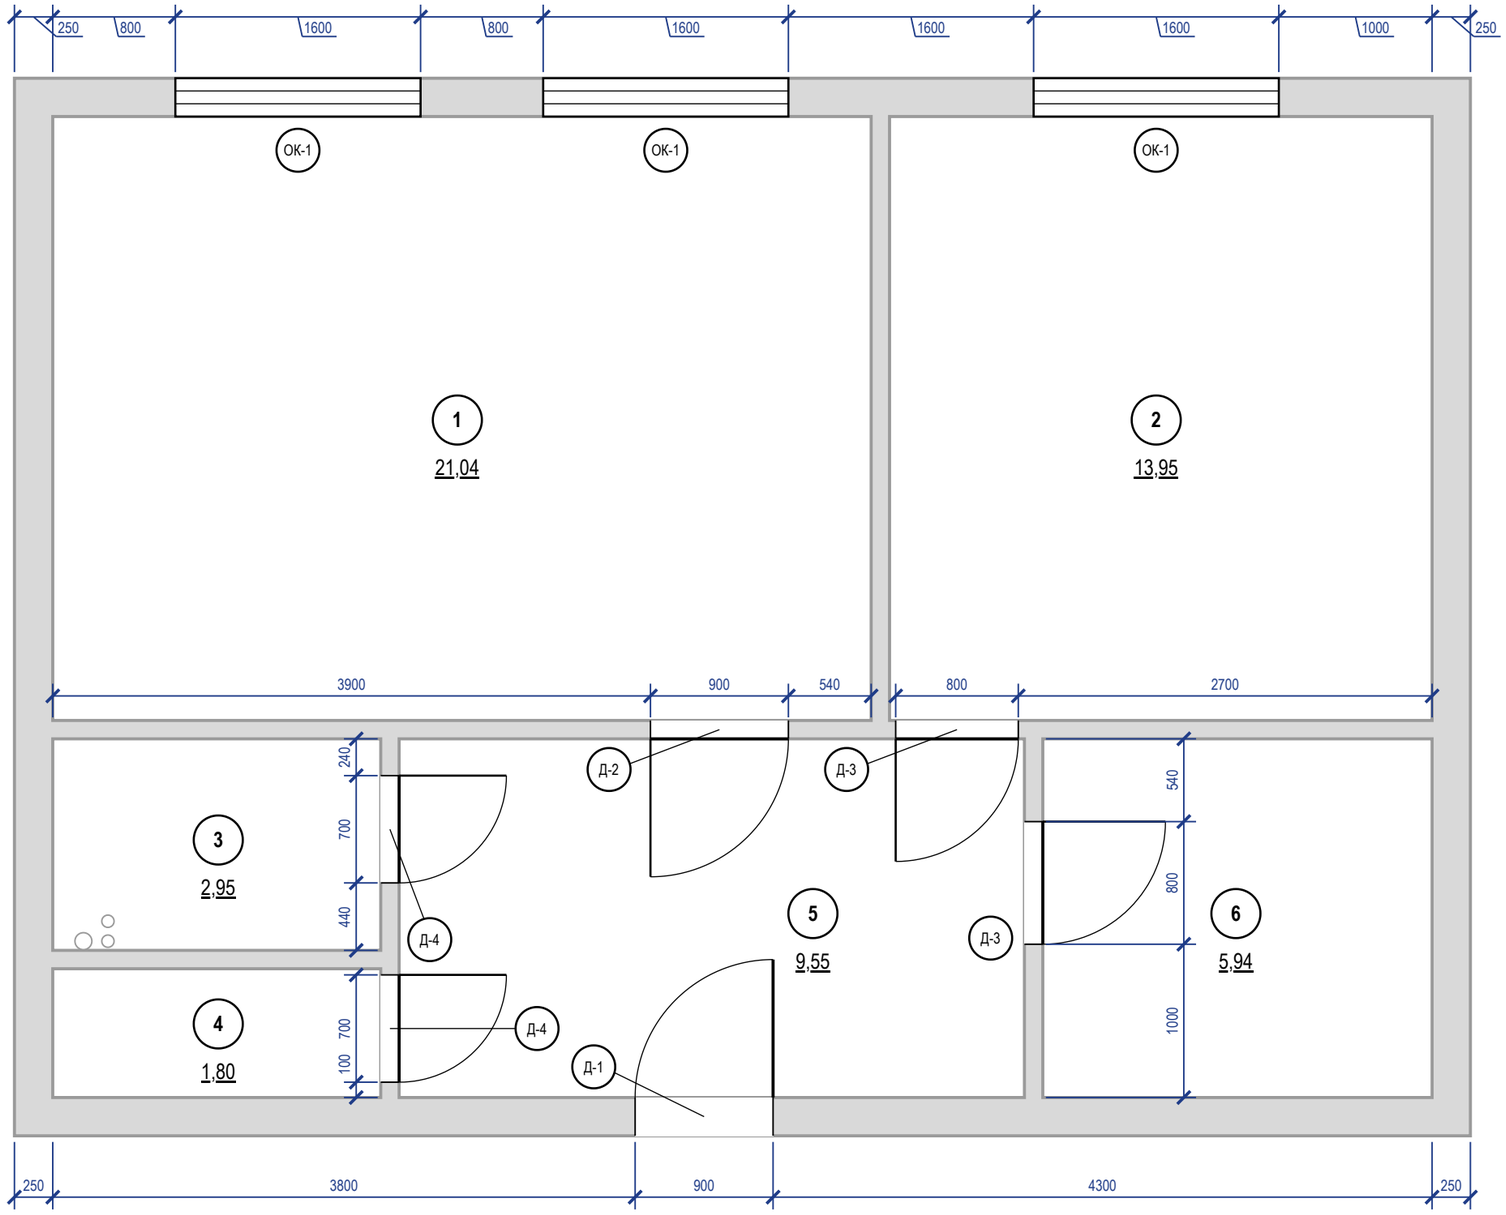

Примечания

1. Размеры проёмов и привязки — в миллиметрах от чистых граней стен до отделки; привязка — от угла того помещения, со стороны которого стоит размер. Размер проёма — ширина × высота от чистого пола 0,000. Размеры на плане — проёмов, не полотен: полотно — в ведомости, коробка — по системе. Откос от угла помещения до проёма с коробкой — не менее 50 мм.
2. Марки в кружках — типы заполнения проёмов (ГОСТ 21.501-2018, п. 5.3.2); одна марка — один типоразмер; количество сверено с планом.
3. Д-2…Д-4 — существующие проёмы, до техзаключения не расширять.
4. Экспликация помещений — лист 14; в марках помещений — номер и площадь, м².
5. Ведомость проёмов — лист 37: заполнение, открывание полотен, заказ и порядок монтажа блоков.
6. Привязка проёма к углу помещения меньше 1 мм на листе, размер на плане не показан: Д-3 — 40 мм; Д-4 — 40 мм.

	Лист	№ док.	Подпись	Дата	Проект: Квартира 58 м²			М 1:40
Дизайнер	Кырлан А.С.			14.11.26	План размещения дверей	Стадия	Лист	Листов
Проверил						П	36	92
Н. контр.								
Утв.								

выпуск 14.11.2026 № 2b6bd7c078 · стр. 36 из 92


Ведомость заполнения проёмов

Марка	Наименование, обозначение	Проём ш×в, мм	Полотно (расч.)	Кол.	Откр.	Отделка полотна	Фурнитура	Прим.
Д-1	Блок дверной входной, ГОСТ 31173-2016	900×2100	блок задать	1	Л	в комплекте блока	в комплекте блока (замки, глазок)	
Д-2	Дверь скрытого монтажа, Софья (SOFIA) Скрытые двери	900×2100	800×2000	1	Л	S 1502-Y50R — пом. 5, S 1002-Y50R — пом. 1	скрытые петли 3D, магнитный замок	
Д-3	Дверь скрытого монтажа, Софья (SOFIA) Скрытые двери	800×2100	700×2000	2	Л, П	окраска S 1502-Y50R с двух сторон; V503 пом. 6, S 1502-Y50R пом. 5	скрытые петли 3D, магнитный замок	
Д-4	Дверь скрытого монтажа, Софья (SOFIA) Скрытые двери	700×2100	600×2000	2	П, П	S 1502-Y50R — пом. 5, в тон облицовки — пом. 3; S 1502-Y50R — пом. 5, в тон облицовки пом. 4	скрытые петли 3D, магнитный замок, фиксатор WC	порог 15
ОК-1	Блок оконный, ГОСТ 23166-2021	1600×1600		3				низ 800

Примечания

1. Марки проёмов — те же, что на плане размещения дверей (лист 36); привязки проёмов — там же.
2. Открывание: Л — петли слева, П — справа, если смотреть со стороны, куда открывается полотно (на себя).
3. Скрытые двери (Д-2…Д-4): проём замерить в чистоте; блок заказать до штукатурки (≈ 30 дн.), короб ставить до штукатурки; полотно навесить после чистовой отделки, красить в цвет стен. Порядок — практика монтажа, изготовитель подтверждает.
4. Полотно «расч.» — по проёму с запасом по каталогам, заказ — по таблице проёмов модели; Д-2…Д-4: проём 2100, а под полотно 2000 по каталогам нужен 2050–2080, под 2100 2150–2180: высоту проёма — по модели; Д-1: входной блок по ГОСТ 31173-2016 — задать при выборе блока.


Схемы дверных блоков (1:25) — вид со стороны открывания; вершина треугольника — сторона петель

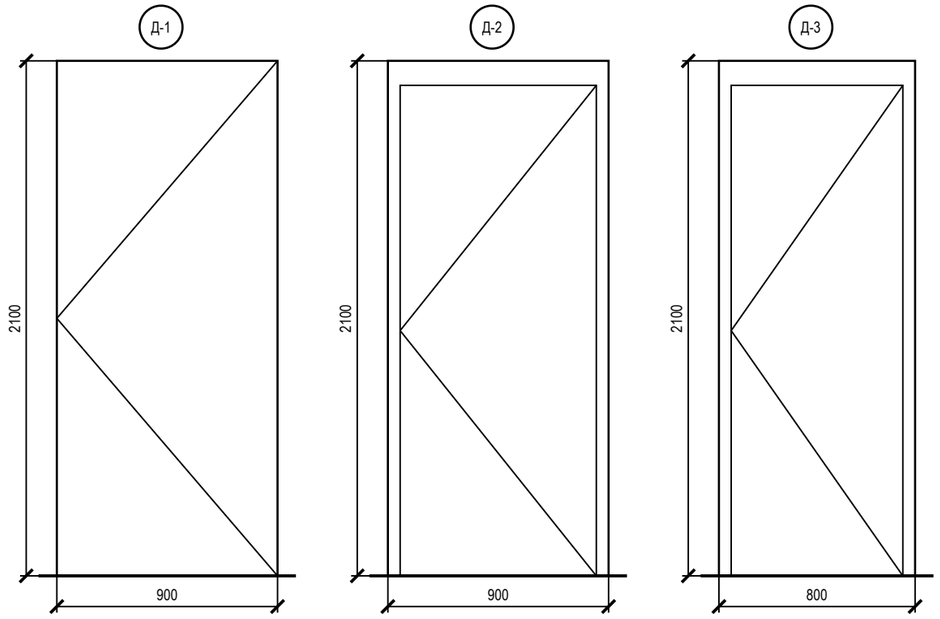

блок — по ГОСТ 31173
откр. Л

полотно 800×2000 (расч.)
откр. Л


полотно 700×2000 (расч.)
откр. Л, П (схема — Л, остальные по плану)

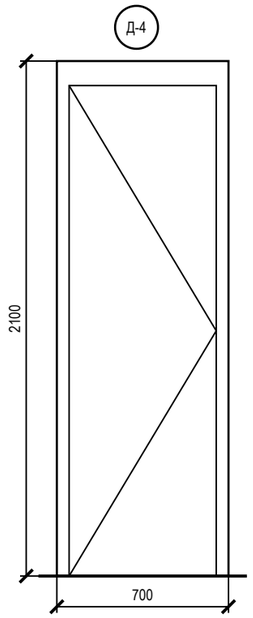

полотно 600×2000 (расч.)
откр. П, П

	Лист	№ док.	Подпись	Дата	Проект: Квартира 58 м²			
Дизайнер	Кырлан А.С.			14.11.26	Ведомость заполнения проёмов	Стадия	Лист	Листов
Проверил						П	37	92
Н. контр.								
Утв.								

выпуск 14.11.2026 № 2b6bd7c078 · стр. 37 из 92

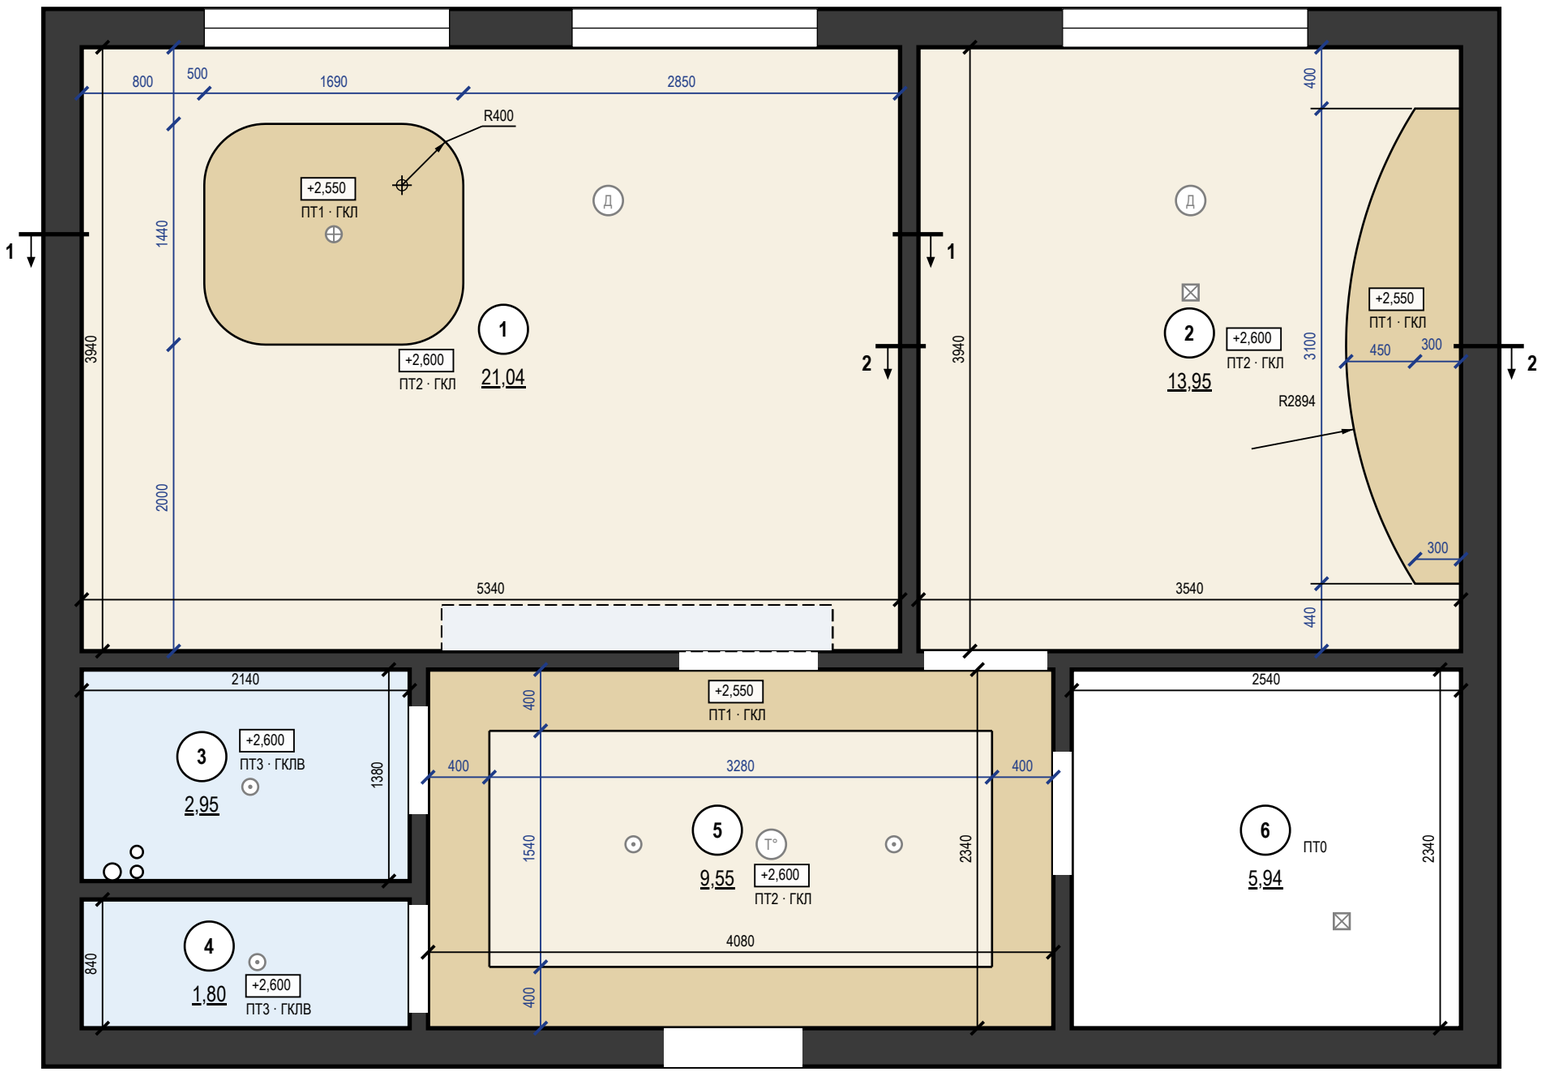

Ведомость потолков

Пом.	Марка	Конструкция	Низ / верх ниши	S, м²	Q
1	ПТ1	ГКЛ П113, остров	+2,550	2,30	Q3
1	ПТ2	ГКЛ П113	+2,600	18,74	Q3
2	ПТ1	ГКЛ П113, дуга	+2,550	1,88	Q3
2	ПТ2	ГКЛ П113	+2,600	12,07	Q3
3	ПТ3	ГКЛВ П113	+2,600	2,95	Q3
4	ПТ3	То же	+2,600	1,80	Q3
5	ПТ1	ГКЛ П113	+2,550	4,50	Q3
5	ПТ2	ГКЛ П113	+2,600	5,05	Q3
6	ПТ0	Существующий потолок, окраска	+2,700	5,94	
		Итого		**55,23**	

Ведомость вырезов и закладных в потолке

Марка	Устройство	Кол.	Пом.
	Светильник встраиваемый (марки — план освещения)	4	3, 4, 5
	Светильник накладной (марки — план освещения)	2	2, 6
	Светильник подвесной (марки — план освещения)	1	1
	Извещатель дымовой	2	1, 2
	Извещатель тепловой	1	5

Примечания


1. За отметку ±0,000 принят уровень чистого пола сухих помещений (готовое покрытие), а не существующего пола; пол пом. 3, 4 — −0,015; верх плиты перекрытия −0,064 — расчётный по пирогу пола, не замерен; существующий пол снимается до плиты, его отметка не замерена. Отметки в прямоугольниках — низ потолка; низ перекрытия +2,700. Марка потолка — одна конструкция и отметка на весь альбом.
2. Размеры помещений в свету (ширина × длина, мм), не поместившиеся на плане: пом. 4 — 2140 × 840.
3. Потолки ГКЛ — каркасная система П113: подвесы через 1000 (с запасом: СП 163, табл. 14 — до 1100 при 0,15 кН/м²), несущие профили через 500, основные через 1200 мм; листы — поперёк несущих профилей. В помещениях 3, 4 — ГКЛВ на оцинкованном каркасе.
4. Нижний уровень — пояс-короб по периметру шириной 400 мм, верхний — поле внутри пояса: пом. 5.
5. Примыкание к стенам: теневой шов 15 мм, техзазор 3 мм — пом. 1, 2, 5, по стенам, выровненным штукатуркой (узел 1); пом. 3, 4 — разделительная лента.
6. Светильники и потолочные устройства — подложка с планов освещения, слаботочных систем и вентиляции (положение — по ним); вырезы и закладные — по ведомости на листе, до обшивки; отверстия не совмещать с профилями, глубина корпуса светильника до 70 мм.
7. Разрезы 1–1, 2–2 — на листе 39; высоты мебели и дверных блоков сверены с низом потолка в разрезах; гибка бортов фигур и ленты ниш — там же; размеры фигурных уровней — фрагменты 1, 2 (лист 40).
8. Шпаклевание ГКЛ и условия приёмки — Q3: рассеянный дневной свет, осмотр с 2 м; боковой свет не оценивается.
9. Пом. 1: короб воздуховода кухонной вытяжки ГКЛ 300×200 мм (ширина от стены × высота), низ +2,500, длина 2,25 м — по трассе плана вентиляции, вдоль стен до входа в канал под воздуховод Ø125; каркас ПН 28×27 по стене и плите, ПП 60×27, лист ГКЛ 12,5.
10. ПТ0 — пом. 6: существующий потолок, окраска, без подвесного потолка, низ +2,700; материал и цвет — по ведомости отделки.

	Лист	№ док.	Подпись	Дата	Проект: Квартира 58 м²			М 1:40
Дизайнер	Кырлан А.С.			14.11.26	План потолков	Стадия	Лист	Листов
Проверил						П	38	92
Н. контр.								
Утв.								

выпуск 14.11.2026 № 2b6bd7c078 · стр. 38 из 92


Разрез 1–1 (М 1:40)

Пом. 1 Кухня-гостиная; линия разреза — план потолков, лист 38

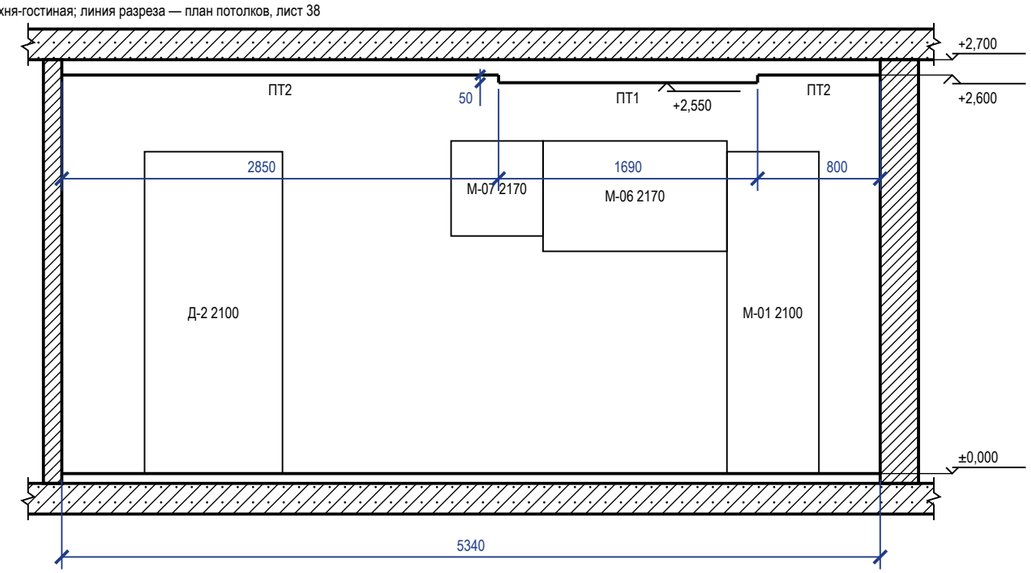

Разрез 2–2 (М 1:40)

Пом. 2 Спальня; линия разреза — план потолков, лист 38

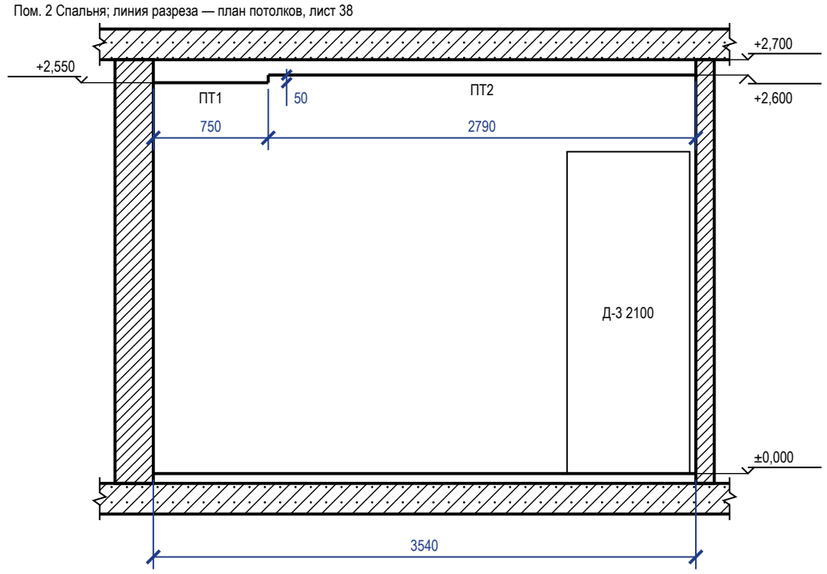

Условные обозначения

- плита перекрытия в сечении
- стена в сечении
- потолок ГКЛ в сечении; под линией — марка потолка (план потолков)
- мебель и дверные проёмы за секущей плоскостью; число — марка и верх от чистого пола, мм

Примечания


1. Разрезы — по линиям 1–1, 2–2 на плане потолков (лист 38). Отметки — от ±0,000 чистого пола, м; размеры — мм.
2. Высоты мебели и дверных блоков за секущей плоскостью сверены с низом потолка над ними: верх ниже низа короба и поля.
3. ГКЛ 12,5 мм по каркасу П113.
4. Толщины плит перекрытия и пирога пола показаны условно.
5. Ведомость объёмов потолков (лист ГКЛ, профиль, подвесы, лента, блоки питания, люки) — на листе 40.
6. Фрагменты 1, 2 — помещения с фигурными уровнями (размеры фигур, радиусы, отметки) — на листе 40.

	Лист	№ док.	Подпись	Дата	Проект: Квартира 58 м²			М 1:40
Дизайнер	Кырлан А.С.			14.11.26				
Проверил					Разрезы и узлы потолков	Стадия	Лист	Листов
Н. контр.						П	39	92
Утв.								

выпуск 14.11.2026 № 2b6bd7c078 · стр. 39 из 92

Фрагмент 1. Пом. 1 Кухня-гостиная — уровни потолка (М 1:50)

Цепочки — от чистых граней стен; отметки — низ уровня от ±0,000

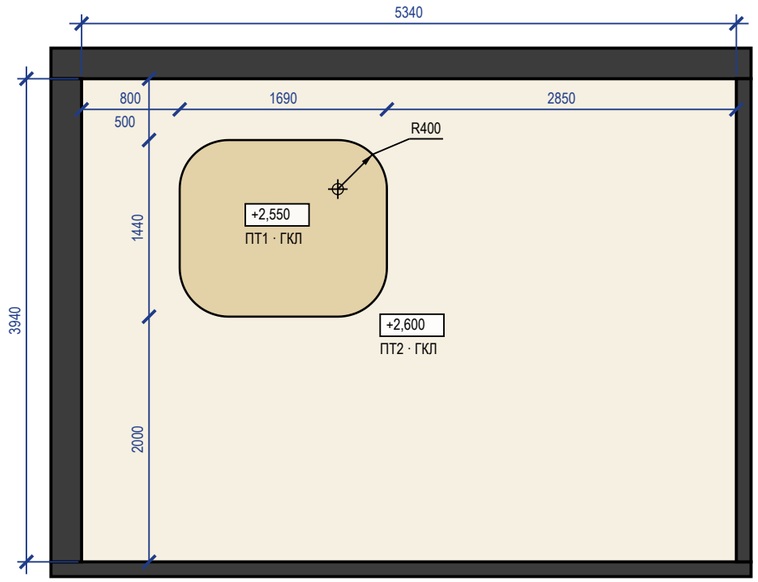


ПТ1 — низ +2,550

ПТ2 — низ +2,600

Фрагмент 2. Пом. 2 Спальня — уровни потолка (М 1:50)

Цепочки — от чистых граней стен; отметки — низ уровня от ±0,000

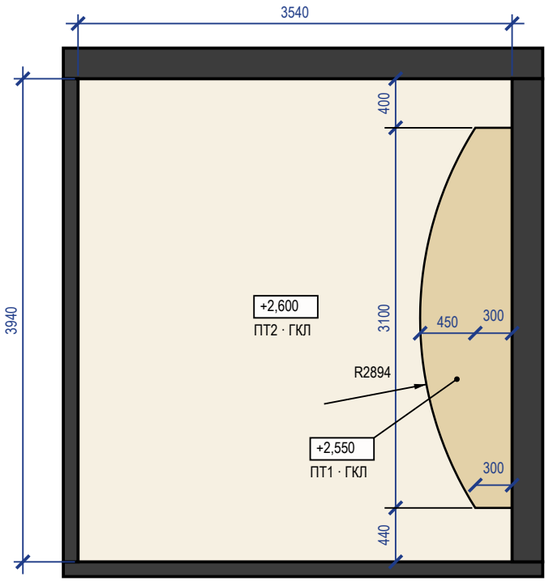

ПТ1 — низ +2,550

ПТ2 — низ +2,600

Ведомость объёмов потолков


Позиция	Ед.	Кол.	Пом.
Лист ГКЛ 12,5	м²	45,36	1, 2, 5
Лист ГКЛВ 12,5	м²	4,75	3, 4
Лист ГКЛ арочный 6,5	м²	0,25	1
Борта и карнизы (входят в площади листов выше)	м²	0,95	1, 2, 5
Профиль ПП 60×27	м	142,49	1, 2, 3, 4, 5
Профиль ПН 28×27	м	97,53	1, 2, 3, 4, 5
Подвес прямой	шт.	55	1, 2, 3, 4, 5
Анкер-клин к плите	шт.	55	1, 2, 3, 4, 5
Шуруп TN 3,5×25	шт.	1156	1, 2, 3, 4, 5
Лента армирующая для швов	м	60,29	1, 2, 3, 4, 5
Шпаклёвка для швов	кг	20,10	1, 2, 3, 4, 5
Грунтовка (швы)	л	5,02	1, 2, 3, 4, 5
Лента разделительная по периметру	м	59,36	1, 2, 3, 4, 5
Сплошная шпаклёвка и окраска (площадь развёртки)	м²	50,24	1, 2, 3, 4, 5

Примечания

1. ГКЛ 12,5 мм по каркасу П113; условные обозначения разрезов — на листе 39.
2. Фрагменты 1, 2 (план потолков — лист 38) — фигурные уровни потолка крупно: привязки краёв и центров фигур к чистым граням стен, радиусы (R) с центрами, хорда и стрелка дуги, отметки низа каждого уровня; цвета уровней — как на плане потолков.
3. Фигурные уровни: борт — ГКЛ по ПН с надрезами (на дуге шаг стоек борта 300 мм при R до 2500, 400 — до 5000) или по гнутому заводскому профилю (СП 163, 6.3.3); гибка: остров пом. 1 R400 — ГКЛ 6,5 мокрой гибкой; дуга пом. 2 R2894 — ГКЛ 12,5 сухой гибкой (СП 163, табл. 9).
4. Ведомость объёмов — по геометрии плана потолков: Лист ГКЛ 12,5 — плоскости уровней + борта (без арочных участков); Лист ГКЛВ 12,5 — плоскости уровней + борта; Лист ГКЛ арочный 6,5 — кривая борта × высота борта и стенки ниши × 2 слоя (R400 мокрая гибка); Борта и карнизы — длина перепада × перепад; Профиль ПП 60×27 — S × (1/шаг несущ. + 1/шаг осн.) + стойки бортов; Профиль ПН 28×27 — периметр стен + 2 × перепады + карнизы; Подвес прямой — по раскладке: S уровня / (шаг осн. × шаг подвесов), пояс уже шага — ряд вдоль пояса, фигура — по контуру; шаг подвесов — не больше табл. 14 СП 163; Анкер-клин к плите — по одному на подвес (Knauf П113); Шуруп TN 3,5×25 — 23 шт./м² (Knauf П113, табл. 2 альбома П 11); Лента армирующая для швов — 1,2 м/м² листа (Knauf); Шпаклёвка для швов — 0,4 кг/м² листа, только швы (Knauf); Грунтовка (швы) — 0,1 л/м² листа, только швы (Knauf); Лента разделительная по периметру — периметр стен под потолком ГКЛ; Сплошная шпаклёвка и окраска (площадь развёртки) — плоскости + борта; расход — по паспорту материала (норма расхода на сплошной слой не подтверждена); без запаса на подрезку (при закупке листа: ×1,075 при S > 20 м², ×1,175 — 10–20 м², ×1,275 — < 10 м²).

	Лист	№ док.	Подпись	Дата	Проект: Квартира 58 м²			М 1:50
Дизайнер	Кырлан А.С.			14.11.26	Разрезы и узлы потолков (продолжение)	Стадия	Лист	Листов
Проверил						П	40	92
Н. контр.								
Утв.								

выпуск 14.11.2026 № 2b6bd7c078 · стр. 40 из 92

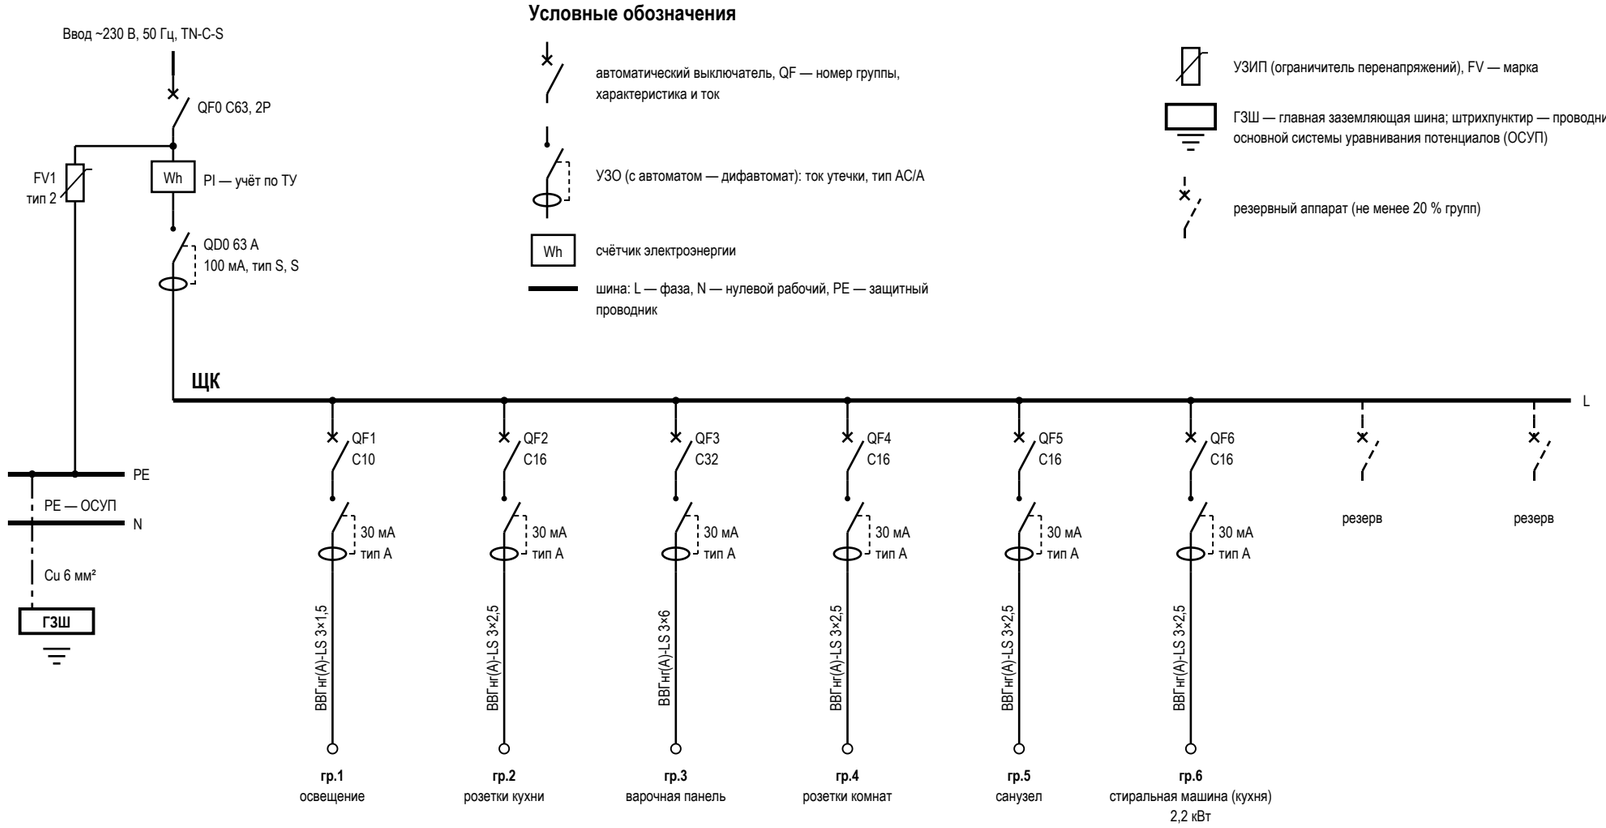

Условные обозначения

автоматический выключатель, QF — номер группы, характеристика и ток

УЗО (с автоматом — дифавтомат): ток утечки, тип AC/A

Wh — счётчик электроэнергии

шина: L — фаза, N — нулевой рабочий, PE — защитный проводник

УЗИП (ограничитель перенапряжений), FV — марка

ГЗШ — главная заземляющая шина; штрихпунктир — проводник основной системы уравнивания потенциалов (ОСУП)

резервный аппарат (не менее 20 % групп)

Данные щитка

Показатель	Значение
Номер щитка	ЩК
Тип	ЩРВ-П-24, IP41
Уст. мощность, кВт	
Разреш. мощность, кВт	15
Расчётная, кВт	9,8
Автоматы 1п: занят. / рез.	6 / 2
Модулей: всего / занято	24 / 19
Ток на вводе, А	63
Вводной аппарат	QF0 C63, 2P
УЗИП	FV1, тип 2, ЩК, после счётчика
ГЗШ, проводник ОСУП	Cu 6 мм²

Таблица групп щита ЩК и кабельный журнал

№	Назначение	Помещения	Автомат	УЗО / дифавтомат	Кабель	Длина, м	Р, кВт	Точек
1	освещение	1, 2, 3, 4, 5, 6	C10	30 мА, тип A	ВВГнг(A)-LS 3×1,5	106,5		25
2	розетки кухни	1	C16	30 мА, тип A	ВВГнг(A)-LS 3×2,5	20,8		4
3	варочная панель	1	C32	30 мА, тип A	ВВГнг(A)-LS 3×6	10,7		1
4	розетки комнат	1, 2, 5	C16	30 мА, тип A	ВВГнг(A)-LS 3×2,5	48,1		11
5	санузел	3	C16	30 мА, тип A	ВВГнг(A)-LS 3×2,5	12		2
6	стиральная машина (кухня)	1	C16	30 мА, тип A	ВВГнг(A)-LS 3×2,5	11	2,2	1
	Итого по сечениям ВВГнг(A)-LS, м: 3×1,5 — 106,5; 3×2,5 — 91,9; 3×6 — 10,7					209,1		

Примечания

1. Схема однолинейная: одна линия — фаза, N и PE группы; аппараты — в отключённом положении (ГОСТ 2.702, ГОСТ 2.755). Номера групп — как у точек на планах (гр.). За отметку 0,000 принят уровень чистого пола; высота щита — по плану розеток.
2. Розеточные и мокрые линии — через УЗО или дифавтомат с током утечки не более 30 мА (ПУЭ 7.1.79); в санузле выполнить ДСУП (ПУЭ 7.1.87–7.1.88).
3. УЗО тип A — для линий с электроникой, стиральной и посудомоечной машиной, LED-драйверами; тип AC — только для чисто активной нагрузки.
4. Кабель — медный, исполнение нг(A)-LS (ГОСТ 31565-2012); скрытая прокладка только горизонтально и вертикально, фактические трассы зафиксировать исполнительной схемой до закрытия отделкой.
5. Номинал автомата — не выше допустимого тока кабеля: 1,5 мм² — до 10 А, 2,5 мм² — до 16 А. Резерв щита — не менее 20 % модулей.
6. Расчёт нагрузок, токов КЗ, селективности и сечений — по проекту ЭОМ организации с допуском СРО; лист задаёт состав, расположение и группы.
7. УЗИП FV1 — после вводного автомата, проводник к шине PE — кратчайший, без петель. Шина PE щита соединяется с ГЗШ проводником ОСУП; к ГЗШ присоединяются трубы водопровода и отопления на вводе в квартиру (ПУЭ 7.1.87). Шины N и PE — раздельные, после разделения PEN не объединяются.
8. До подключения нагрузки — приёмо-сдаточные испытания с протоколом: сопротивление изоляции линий не менее 0,5 МОм, срабатывание УЗО по току и времени, непрерывность защитных проводников PE (ПУЭ, гл. 1.8).

	Лист	№ док.	Подпись	Дата	Проект: Квартира 58 м²			
Дизайнер	Кырлан А.С.			14.11.26	Однолинейная схема щита	Стадия	Лист	Листов
Проверил						П	41	92
Н. контр.								
Утв.								

Группы щита ЩК (1)

№	Назначение	Руст, кВт	Кс	Ррасч, кВт	Iрасч, А	Автомат	Кабель
1	освещение	0	0,6	0	0	C10	3×1,5
2	розетки кухни	0	0,4	0	0	C16	3×2,5
3	варочная панель	0	0,6	0	0	C32	3×6

Группы щита ЩК (2)

№	Назначение	Руст, кВт	Кс	Ррасч, кВт	Iрасч, А	Автомат	Кабель
4	розетки комнат	0	0,4	0	0	C16	3×2,5
5	санузел	0	0,7	0	0	C16	3×2,5
6	стиральная машина (кухня)	2,2	0,7	1,54	7	C16	3×2,5

Итог по квартире

Показатель	Значение
Установленная мощность Σ Руст	2,2 кВт
Σ Руст × Кс по группам	1,54 кВт
Коэффициент одновременности	0,7
Расчётная мощность квартиры Ррасч	1,1 кВт
Расчётный ток Iрасч (230 В, cosφ 0,95)	5 А
Разрешённая мощность	15 кВт
Запас до разрешённой	92,8 %
Вводной аппарат	C63, 2P


Примечания

1. Руст — установленная мощность группы по данным щита (приборы — по паспорту, розетки общего назначения — оценка 0,1 кВт на гнездо). Кс — коэффициенты спроса: освещение 0,6; розетки 0,4; варочная и духовой 0,6; кондиционеры 0,8; тёплый пол 1,0; прочие 0,7; одновременность 0,7.
2. Коэффициенты — ориентир исполнителя, не табличные значения нормы; расчёт нагрузки подтверждает инженер ЭОМ (СП 256.1325800.2016). Под разрешённую мощность они не подгоняются.
3. Вывод: запас 93 % (расчётная 1,1 кВт при разрешённой 15 кВт).
4. Розеточные и мокрые линии — через УЗО или дифавтомат с током утечки не более 30 мА (ПУЭ 7.1.79); в санузле выполнить ДСУП (ПУЭ 7.1.87–7.1.88).

	Лист	№ док.	Подпись	Дата	Проект: Квартира 58 м²			
Дизайнер	Кырлан А.С.			14.11.26	Таблица нагрузок щита	Стадия	Лист	Листов
Проверил						П	42	92
Н. контр.								
Утв.								

выпуск 14.11.2026 № 2b6bd7c078 · стр. 42 из 92

План принципиальных трасс (М 1:50)

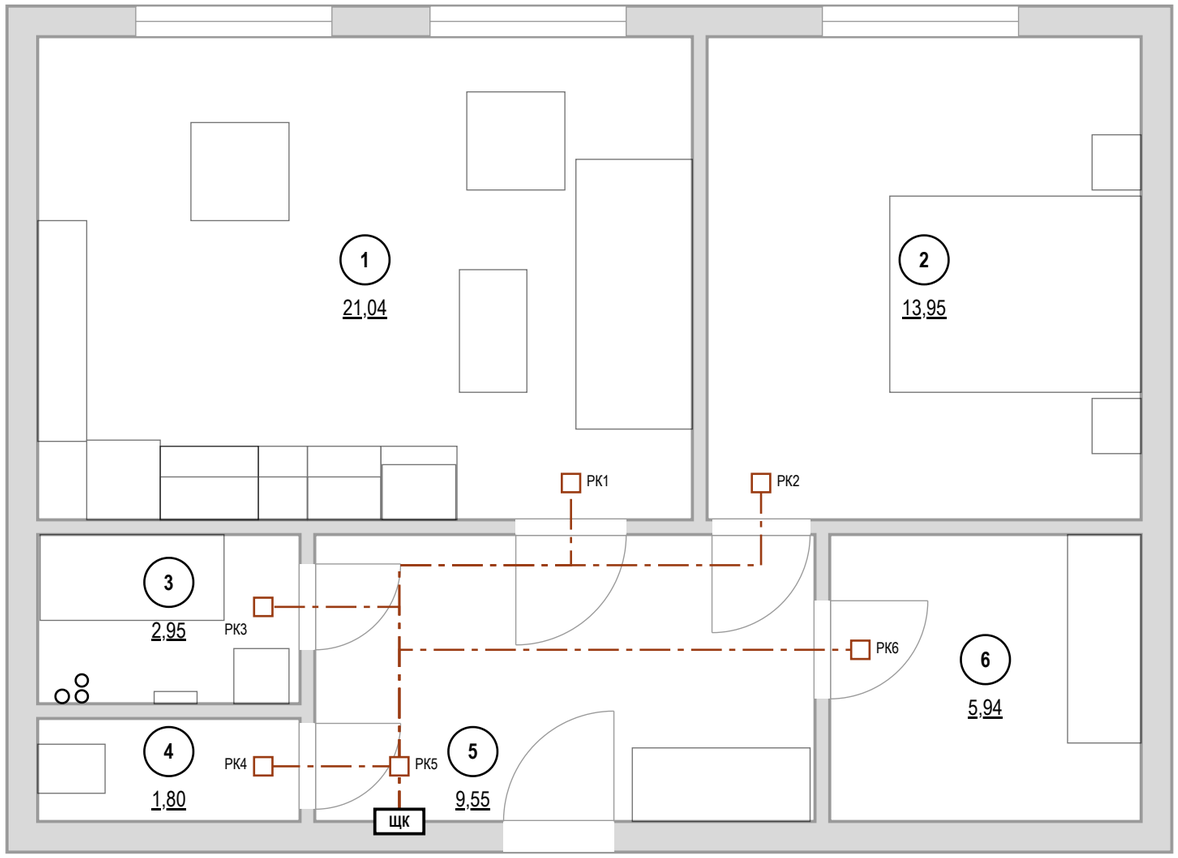

Кабель по группам ВВГнг(А)-LS, м

Гр.	мм²	Трасса	Данные
1	3×1,5	106,5	
2	3×2,5	20,8	
3	3×6	10,7	

Гр.	мм²	Трасса	Данные
4	3×2,5	48,1	
5	3×2,5	12	
6	3×2,5	11	
Σ		**209,1**	

Экспликация помещений

№	Помещение	Площадь, м²
1	Кухня-гостиная	21,04
2	Спальня	13,95
3	Ванная	2,95
4	Санузел	1,80
5	Прихожая	9,55
6	Гардеробная	5,94
	Итого (общая площадь)	55,23

Объёмы прокладки

Работа, материал	Ед.	Кол.
Гофротруба Ø20 в потолочном пространстве	м	72,6
Кабель-канал плинтуса для силовых линий	м	55,8
Короб или накладной канал для вертикальных спусков и подъёмов	м	44,2
Коробка распределительная (РК) над дверью помещения	шт	6
Слаботочка: кабель домофона	м	3,4
Слаботочка: Кабель коаксиальный RG-6 (75 Ом) к розеткам ТВ	м	16,3
Слаботочка: Кабель U/UTP кат. 5е (LAN, Wi-Fi и камеры по PoE)	м	30,1
Слаботочка: гофротруба Ø20 отдельно от силовых	м	44,8

Штробы — только после заключения

Работа	Ед.	Кол.
Вертикальные штробы 20×20 мм от потолка до каждой настенной точки (в маршрут без штроб не входят)	м	58,99

Условные обозначения

- **ЩК** — щит квартирный
- РК — распределительная коробка над дверью помещения
- магистраль от щита к РК: потолочное пространство, гофра
- мебель и сантехприборы — подложка


Примечания

1. За отметку 0,000 принят уровень чистого пола. Высоты Н — от чистого пола до оси изделия; привязки — от чистовой грани стены до оси механизма (у рамки на несколько постов — до оси рамки).
2. Розеточные и мокрые линии — через УЗО или дифавтомат с током утечки не более 30 мА (ПУЭ 7.1.79); в санузле выполнить ДСУП (ПУЭ 7.1.87–7.1.88).
3. Кабель — медный, исполнение нг(А)-LS (ГОСТ 31565-2012); скрытая прокладка только горизонтально и вертикально, фактические трассы зафиксировать исполнительной схемой до закрытия отделкой.
4. Расчёт нагрузок, токов КЗ, селективности и сечений — по проекту ЭОМ организации с допуском СРО; лист задаёт состав, расположение и группы.
5. Длины — по плану: от щита вверх в потолочное пространство, по дверям и коридору без захода в мокрые помещения к распределительной коробке над дверью, далее к точкам; вертикали считаются вниз и обратно (у последней точки цепочки — в один конец); запас 10 %. Трассы принципиальные: фактическую зафиксировать исполнительной схемой до закрытия отделкой.
6. Несущие стены не определены: штробы в стенах не выполнять. Маршрут проложен без штроб: горизонтали — за потолком в гофре (72,6 м) и в кабель-канале плинтуса (55,8 м), вертикали — в коробе или накладном канале (77,8 м кабеля). Точек: за потолком — 9, спуск из потолка — 7, по плинтусу — 11, плинтус и подъём — 18.
7. Вариант со штробами — работа после технического заключения: 58,99 м вертикальных штроб от потолка до каждой настенной точки; условие — только после технического заключения: стена не несущая (или вертикальная штроба в несущей согласована конструктором), глубина и ширина 20–25 мм, не в зонах 0–2 ванной. Без заключения и согласования конструктора в смету и в график эта работа не входит.
8. Слаботочные сети: кабели и точки считаются по лучам от ЩС (лист слаботочных сетей): 50 м, портов патч-панели и коммутатора не менее 2. Изделия — в ведомости изделий.

	Лист	№ док.	Подпись	Дата	Проект: Квартира 58 м²			М 1:50
Дизайнер	Кырлан А.С.			14.11.26	План принципиальных трасс	Стадия	Лист	Листов
Проверил						П	43	92
Н. контр.								
Утв.								

выпуск 14.11.2026 № 2b6bd7c078 · стр. 43 из 92

План розеток (М 1:40)

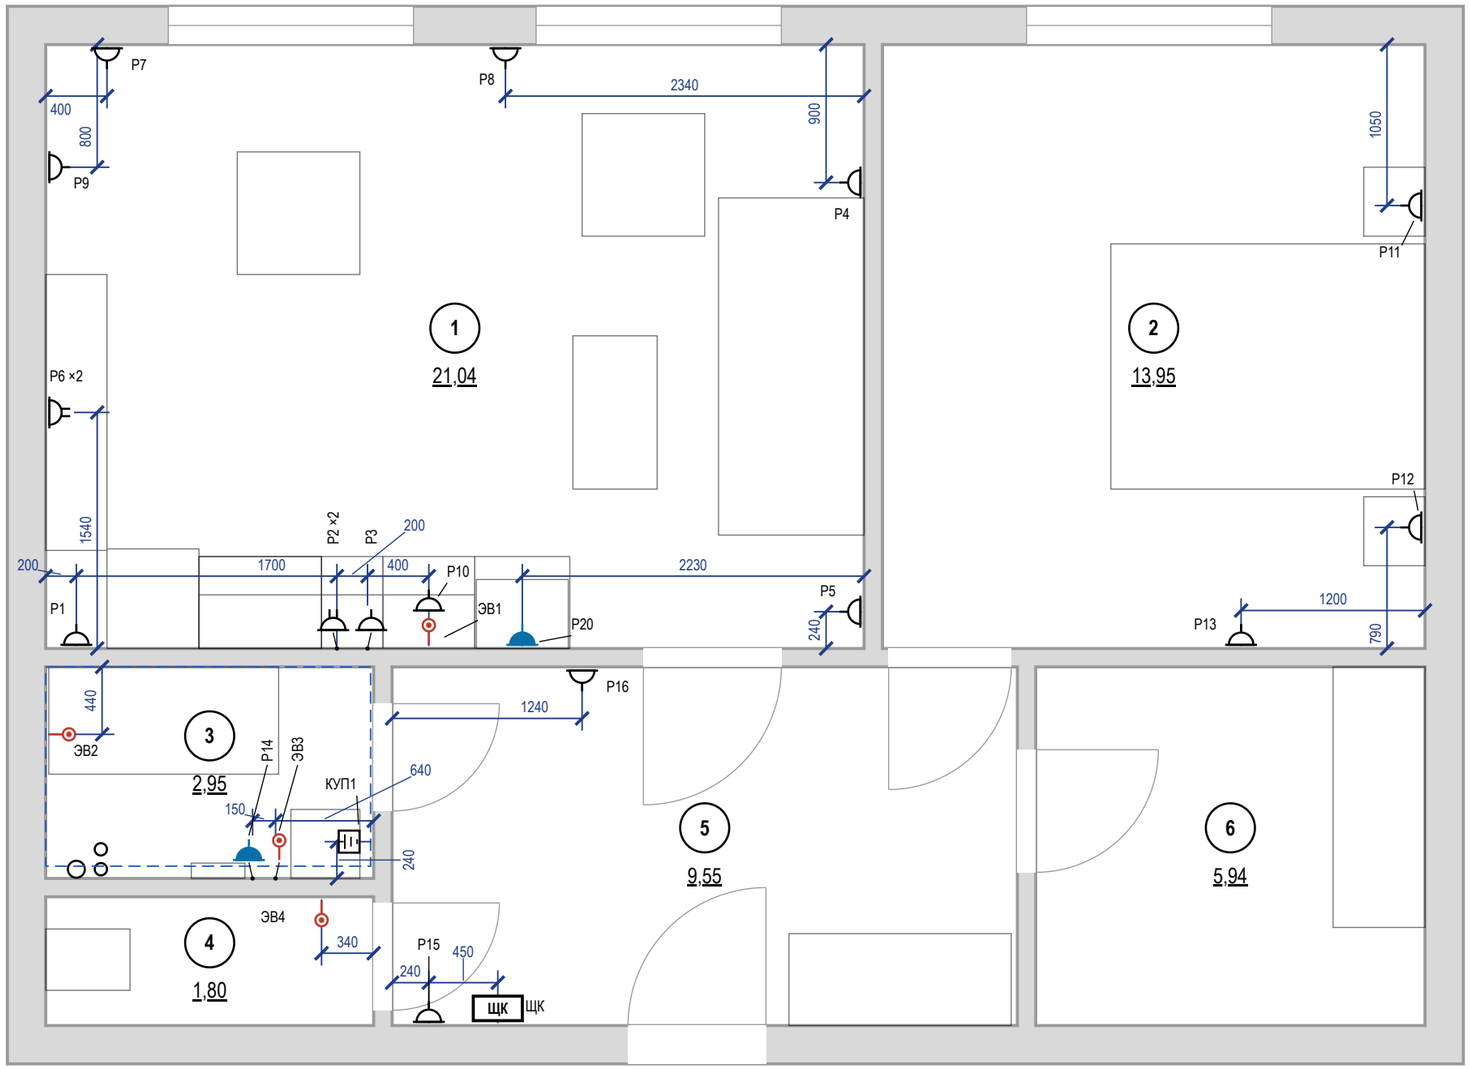

Условные обозначения

Знак	Тип изделия	Н, мм	Кол., шт
	Розетка с заземлением	300	9
	То же	у знака	4
	Блок розеток с заземлением, рамка 2 поста	у знака	2
	Розетка с заземлением IP44	1100	2
	Вывод кабеля к прибору	у знака	4
	КУП (уравнивание потенциалов)	300	1
ЩК	Щит квартирный	1700	1

- розетка с заземляющим контактом; у знака — марка и ×N — число постов в рамке; группа щита, высота оси и назначение — в ведомости точек
- знак разведён для читаемости: точка на стене — у выноски, привязка — до неё
- граница зоны 2 ванной (600 мм от ванны/поддона)
- мебель и сантехприборы — подложка
- стояк: К1 — канализация, В1 — ХВС, Т3 — ГВС
- 1 — номер помещения, площадь м²

Итого розеток (механизмов) — 19 шт; рамок — 17 шт: на 1 пост — 15, на 2 поста — 2.

Примечания


1. За отметку 0,000 принят уровень чистого пола. Высоты Н — от чистого пола до оси изделия; привязки — от чистовой грани стены до оси механизма (у рамки на несколько постов — до оси рамки).
2. Высоты Н и группы щита — в ведомости электроточек: розетки — 300 мм от чистого пола до оси механизма, если в ведомости не указано иное; выводы кабеля — по паспорту прибора.
3. Розетки в санузле — только вне зон 0–2 (ПУЭ 7.1.48, ГОСТ Р 50571.7.701-2024), IP44, через УЗО 30 мА.
4. Розеточные и мокрые линии — через УЗО или дифавтомат с током утечки не более 30 мА (ПУЭ 7.1.79); в санузле выполнить ДСУП (ПУЭ 7.1.87–7.1.88).
5. Кабель — медный, исполнение нг(А)-LS (ГОСТ 31565-2012); скрытая прокладка только горизонтально и вертикально, фактические трассы зафиксировать исполнительной схемой до закрытия отделкой.
6. Расчёт нагрузок, токов КЗ, селективности и сечений — по проекту ЭОМ организации с допуском СРО; лист задаёт состав, расположение и группы.
7. Выводы кухонной техники — после утверждения проекта кухни (ориентировочно); привязки выводов даны от осей модулей гарнитура и пересматриваются вместе с проектом кухни.

	Лист	№ док.	Подпись	Дата	Проект: Квартира 58 м²			М 1:40
Дизайнер	Кырлан А.С.			14.11.26	План розеток и электровыводов	Стадия	Лист	Листов
Проверил						П	44	92
Н. контр.								
Утв.								

План слаботочных сетей (М 1:40)

Условные обозначения

- ЩС — щит слаботочный: ввод провайдера, роутер, коммутатор
- ПК — розетка компьютерная RJ45
- ТВ — розетка телевизионная
- ДФ — трубка или монитор домофона
- кабель от ЩС до точки, отдельным лучом
- мебель и сантехприборы подложка
- стояк: К1 — канализация, В1 — ХВС, Т3 — ГВС
- 1 — номер помещения, площадь м²

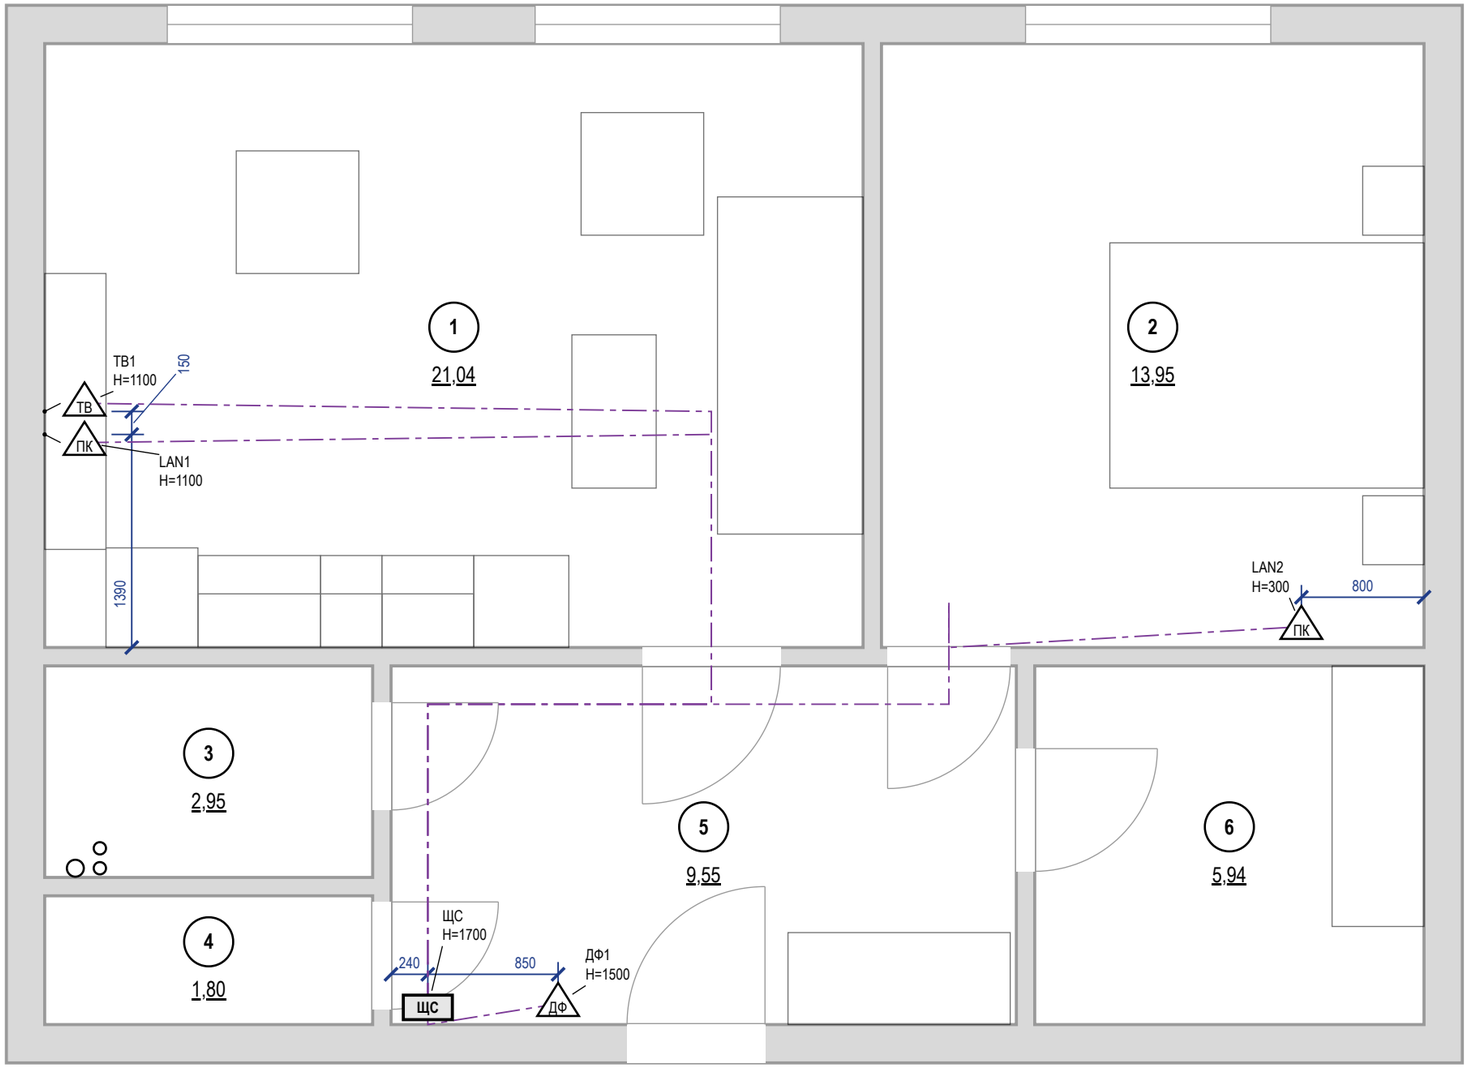

Примечания

1. За отметку 0,000 принят уровень чистого пола. Высоты Н — от чистого пола до оси изделия; привязки — от чистовой грани стены до оси механизма (у рамки на несколько постов — до оси рамки).
2. Высота установки, не указанная на плане: розетки LAN и ТВ — 300 мм от чистого пола.
3. Слаботочные кабели — отдельно от силовых: в своей трубе или лотке, при параллельной прокладке не ближе 100 мм к силовым, пересечения под прямым углом; каждую точку — отдельным кабелем от ЩС без скруток.
4. Трассы на листе — принципиальные; фактические зафиксировать исполнительной схемой до закрытия отделкой. Силовые линии, УЗО 30 мА, ДСУП, кабель нг(А)-LS — по листам розеток и щита.
5. Проект силовой части и расчёт токов КЗ — по проекту ЭОМ; слаботочная часть согласуется с провайдером и управляющей компанией (домофон, коллективное ТВ).

	Лист	№ док.	Подпись	Дата
Дизайнер	Кырлан А.С.			14.11.26
Проверил				
Н. контр.				
Утв.				

Проект: Квартира 58 м² — **М 1:40**

План слаботочных сетей


Стадия	Лист	Листов
П	45	92

выпуск 14.11.2026 № 2b6bd7c078 · стр. 45 из 92

План освещения (М 1:40)

Условные обозначения

- светильник встраиваемый точечный
- светильник потолочный накладной
- светильник подвесной
- светильник настенный (бра), H — высота оси
- линейный светильник настенный (подсветка столешницы), точка — вывод питания
- трековая система
- Св1·L1 — марка светильника (как в ведомости и на развёртках) · группа включения L (лист 48)

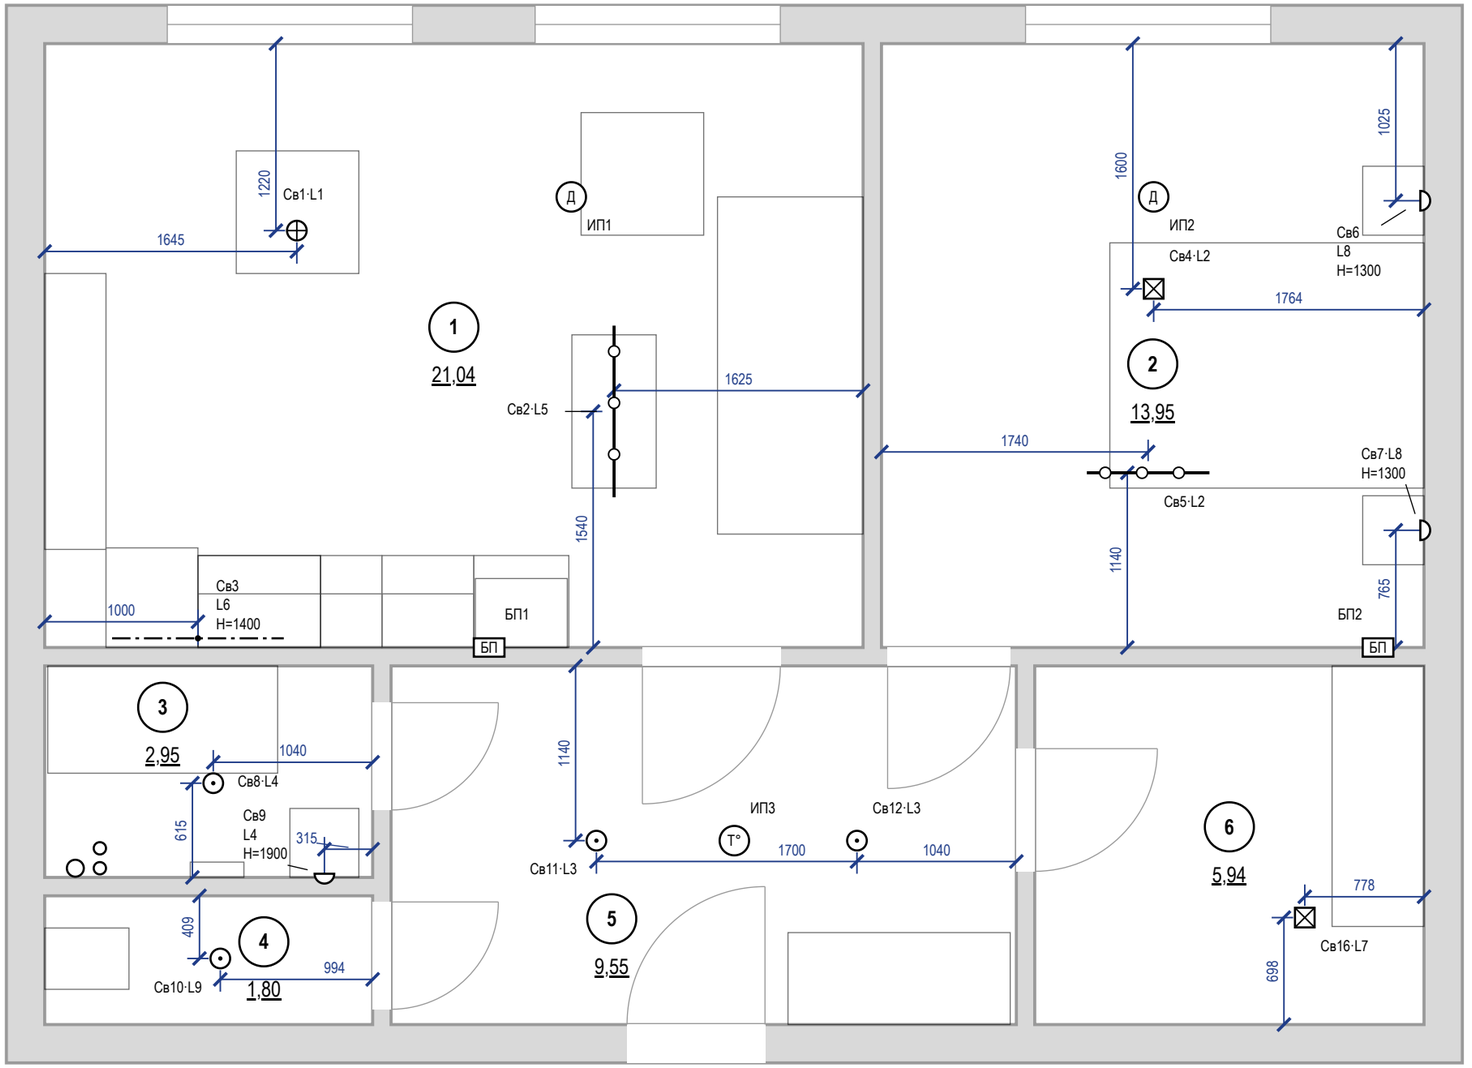

Примечания

1. За отметку 0,000 принят уровень чистого пола. Высоты H — от чистого пола до оси изделия; привязки — от чистовой грани стены до оси механизма (у рамки на несколько постов — до оси рамки).
2. Высота установки, не указанная на плане: светильники — на потолке; настенные — по отметке H у знака. Привязки — до оси светильника от чистовой грани стены, по рядам.
3. Во влажных помещениях — светильники не ниже IP44; в зонах 0–2 ванной — по ГОСТ Р 50571.7.701-2024 (зона 1 — IPX5).
4. Розеточные и мокрые линии — через УЗО или дифавтомат с током утечки не более 30 мА (ПУЭ 7.1.79); в санузле выполнить ДСУП (ПУЭ 7.1.87–7.1.88).
5. Кабель — медный, исполнение нг(A)-LS (ГОСТ 31565-2012); скрытая прокладка только горизонтально и вертикально, фактические трассы зафиксировать исполнительной схемой до закрытия отделкой.
6. Расчёт нагрузок, токов КЗ, селективности и сечений — по проекту ЭОМ организации с допуском СРО; лист задаёт состав, расположение и группы.
7. Ведомость светильников (тип, количество, мощность, поток, Tц, Ra) — лист 47.

Условные обозначения (окончание)

- Д — извещатель пожарный дымовой автономный
- T° — извещатель пожарный тепловой
- БП — блок питания LED, с доступом (люк от 100×100 мм)
- мебель и сантехприборы — подложка
- стояк: К1 — канализация, В1 — ХВС, Т3 — ГВС
- 1 — номер помещения, площадь м²

	Лист	№ док.	Подпись	Дата	Проект: Квартира 58 м²			М 1:40
Дизайнер	Кырлан А.С.			14.11.26	План освещения	Стадия	Лист	Листов
Проверил						П	46	92
Н. контр.								
Утв.								

выпуск 14.11.2026 № 2b6bd7c078 · стр. 46 из 92

Параметры светильников для подбора

Поз.	Марки	Наименование	Установка	Кол.	P, Вт	Σ P, Вт	Ф, лм	Тц, К	Ra	Угол, °	IP	Дим.	Слой	Группа	Пом.
1	Св1	Подвесной	подвес, низ H=1450	1	40	40	3600	3000	90	—	20	—	общий	L1	1
2	Св2	Трековая система	на потолке	4	12	48	950	3000	90	—	20	—	общий	L5	1
3	Св3	Линейный настенный	под верхними шкафами, H=1400	1	14	14	1080	3000	90	—	20	—	рабочий	L6	1
4	Св4	Потолочный накладной	на потолке	1	36	36	3200	2700	90	—	20	—	общий	L2	2
5	Св5	Трековая система	на потолке	2	12	24	900	2700	90	—	20	—	общий	L2	2
6	Св6, Св7	Настенный (бра)	на стене, H=1300	2	4	8	250	2700	90	—	20	—	рабочий	L8	2
7	Св8	Встраиваемый точечный	в ГКЛ, корпус ≤ 70 мм	1	9	9	700	3000	90	—	44	—	общий	L4	3
8	Св9	Настенный (бра)	над зеркалом, H=1900	1	6	6	400	3000	90	—	44	—	рабочий	L4	3
9	Св10	Встраиваемый точечный	в ГКЛ, корпус ≤ 70 мм	1	6	6	500	3000	90	—	44	—	общий	L9	4
10	Св11, Св12	Встраиваемый точечный	в ГКЛ, корпус ≤ 70 мм	2	9	18	800	3000	90	—	20	—	общий	L3	5
11	Св16	Потолочный накладной	на потолке, засветка стены	1	10	10	900	3000	90	—	20	—	общий	L7	6
		Итого		**17 шт**		**219**									

LED-ленты, линейные светильники и блоки питания

Марка	Пом.	L, м	U, В	Вт/м	Σ P, Вт	БП	P БП, Вт	Загр., %	Питание	Доступ к БП
Св2	1	1,2	24	—	48	БП1	100	62	встроенный ввод	H=2300
—	1	1,8	24	—	14	БП1	100	62	встроенный ввод	H=2300
Св5	2	0,8	24	—	24	БП2	60	40	встроенный ввод	H=2300

Примечания

1. Позиции и марки Св — те же, что на плане освещения (лист 46); группы L — по плану выключателей (лист 48).
2. Модели светильников не выбраны: лист — техническое задание на подбор. Модель по строке таблицы: поток, Тц, Ra, угол, IP и регулировка яркости не хуже указанных, мощность не больше; встраиваемые — под глубину короба (графа «Установка»). IP 20 — сухие помещения. После выбора моделей (артикул, производитель) лист выпускается как «Спецификация светильников».
3. Мощность и поток в таблице — требования к подбору (поток не меньше, мощность не больше указанных); после выбора модели — по её паспорту, Σ P — установленная мощность освещения. Оценка освещённости — на плане освещения; это не светотехнический расчёт.


	Лист	№ док.	Подпись	Дата	Проект: Квартира 58 м²			
Дизайнер	Кырлан А.С.			14.11.26				
Проверил					Техническое задание на подбор светильников	Стадия	Лист	Листов
Н. контр.								
Утв.						П	47	92

выпуск 14.11.2026 № 2b6bd7c078 · стр. 47 из 92

План выключателей (М 1:40)

Условные обозначения

- выключатель одноклавишный
- выключатель с проходной или перекрёстной клавишей (обратный флажок); тип клавиши — в подписи
- S1 → — марка → группы по клавишам (через «;»): прох. — проходной, перекр. — перекрёстный, дим. светорегулятор; H — высота
- связь: выключатель → ближайший светильник группы в том же помещении (не трасса кабеля); полный состав группы — по номеру L
- светильник встраиваемый точечный
- светильник потолочный накладной
- светильник подвесной

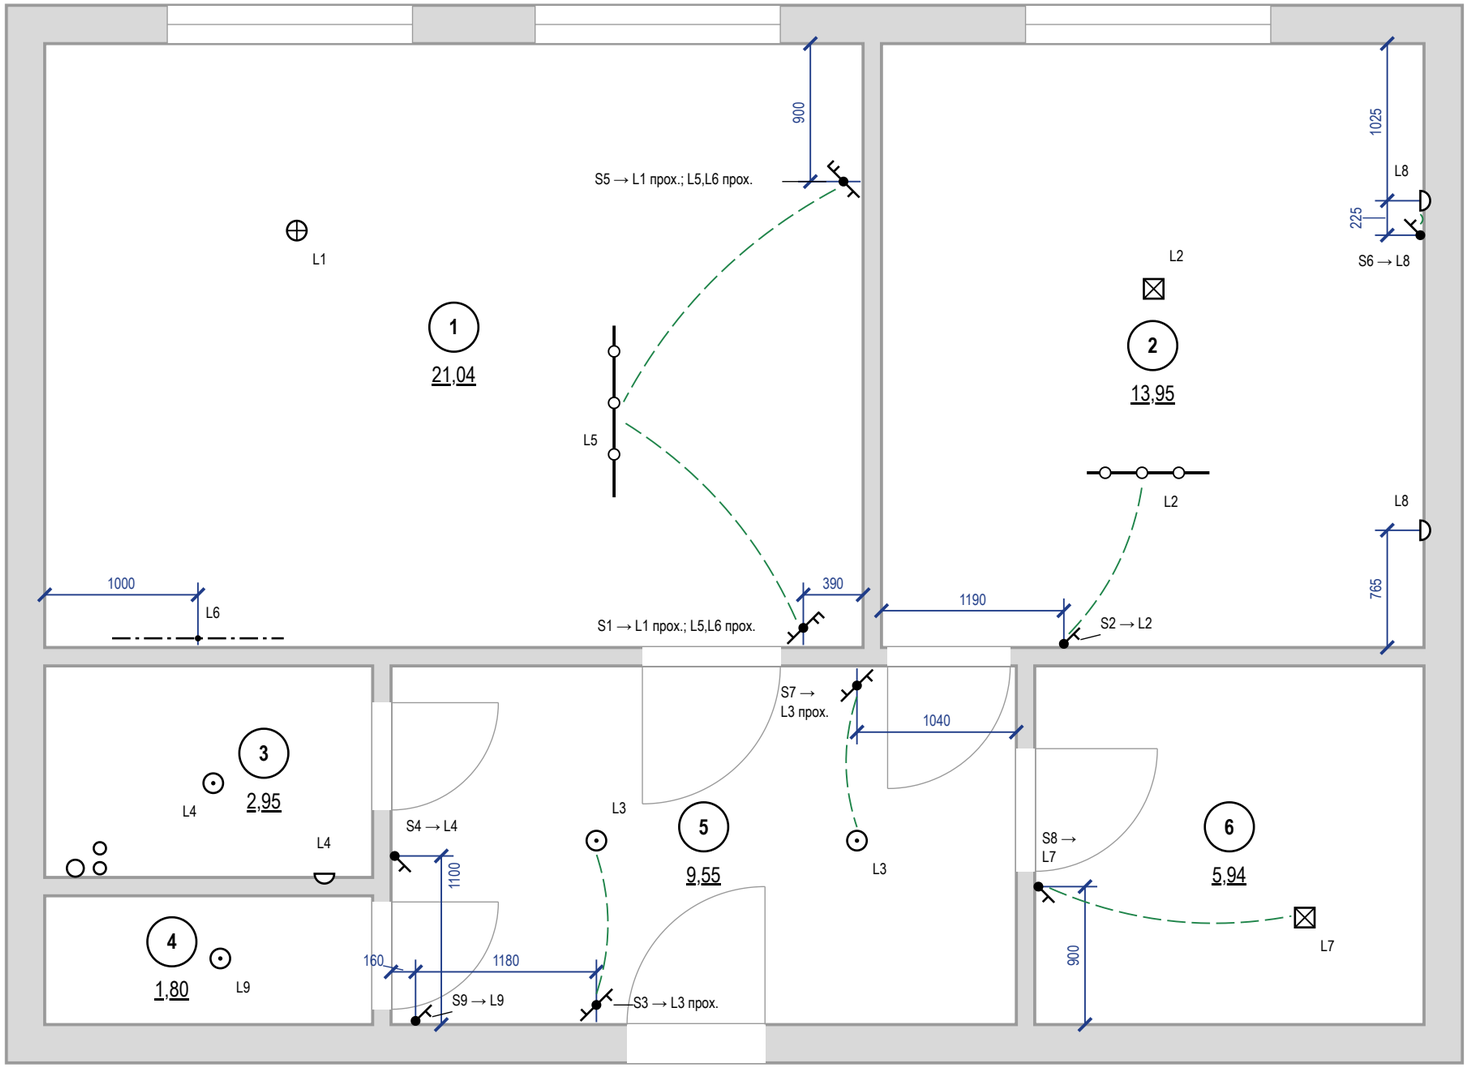

Примечания

1. За отметку 0,000 принят уровень чистого пола. Высоты H — от чистого пола до оси изделия; привязки — от чистовой грани стены до оси механизма (у рамки на несколько постов — до оси рамки).
2. Высота установки, не указанная на плане: выключатели — 900 мм от чистого пола (у кровати и другие — H у марки), со стороны дверной ручки (ПУЭ 7.1.51).
3. Какой выключатель какие светильники включает — по номеру группы L: у выключателя (S1 → L1; L2 — клавиши по порядку) и у каждого светильника. Пунктир подсказка к ближайшему светильнику группы в том же помещении (не дальше 3 м), это не трасса кабеля; выключатель за стеной (у двери санузла) и далёкая группа — только номер группы.
4. Группы из нескольких мест (L1 — S1, S5; L5 — S1, S5; L6 — S1, S5; L3 — S3, S7): на крайних местах — проходные клавиши, на промежуточных — перекрёстные; механизмы — в ведомости изделий.
5. Вентиляторы санузлов (выводы ЭВ на плане розеток) включаются вместе с основным светом помещения, отключаются с задержкой — таймер выбега в вентиляторе.
6. Розеточные и мокрые линии — через УЗО или дифавтомат с током утечки не более 30 мА (ПУЭ 7.1.79); в санузле выполнить ДСУП (ПУЭ 7.1.87–7.1.88).
7. Кабель — медный, исполнение нг(A)-LS (ГОСТ 31565-2012); скрытая прокладка только горизонтально и вертикально, фактические трассы зафиксировать исполнительной схемой до закрытия отделкой.
8. Расчёт нагрузок, токов КЗ, селективности и сечений — по проекту ЭОМ организации с допуском СРО; лист задаёт состав, расположение и группы.


Условные обозначения (окончание)

- светильник настенный (бра), H — высота оси
- линейный светильник настенный (подсветка столешницы), точка — вывод питания
- трековая система
- L1 — группа включения у светильника
- стояк: К1 — канализация, В1 — ХВС, Т3 — ГВС
- 1 — номер помещения, площадь м²

	Лист	№ док.	Подпись	Дата	Проект: Квартира 58 м²			М 1:40
Дизайнер	Кырлан А.С.			14.11.26	Управление светильниками	Стадия	Лист	Листов
Проверил						П	48	92
Н. контр.								
Утв.								

выпуск 14.11.2026 № 2b6bd7c078 · стр. 48 из 92

План вентиляции (М 1:40)

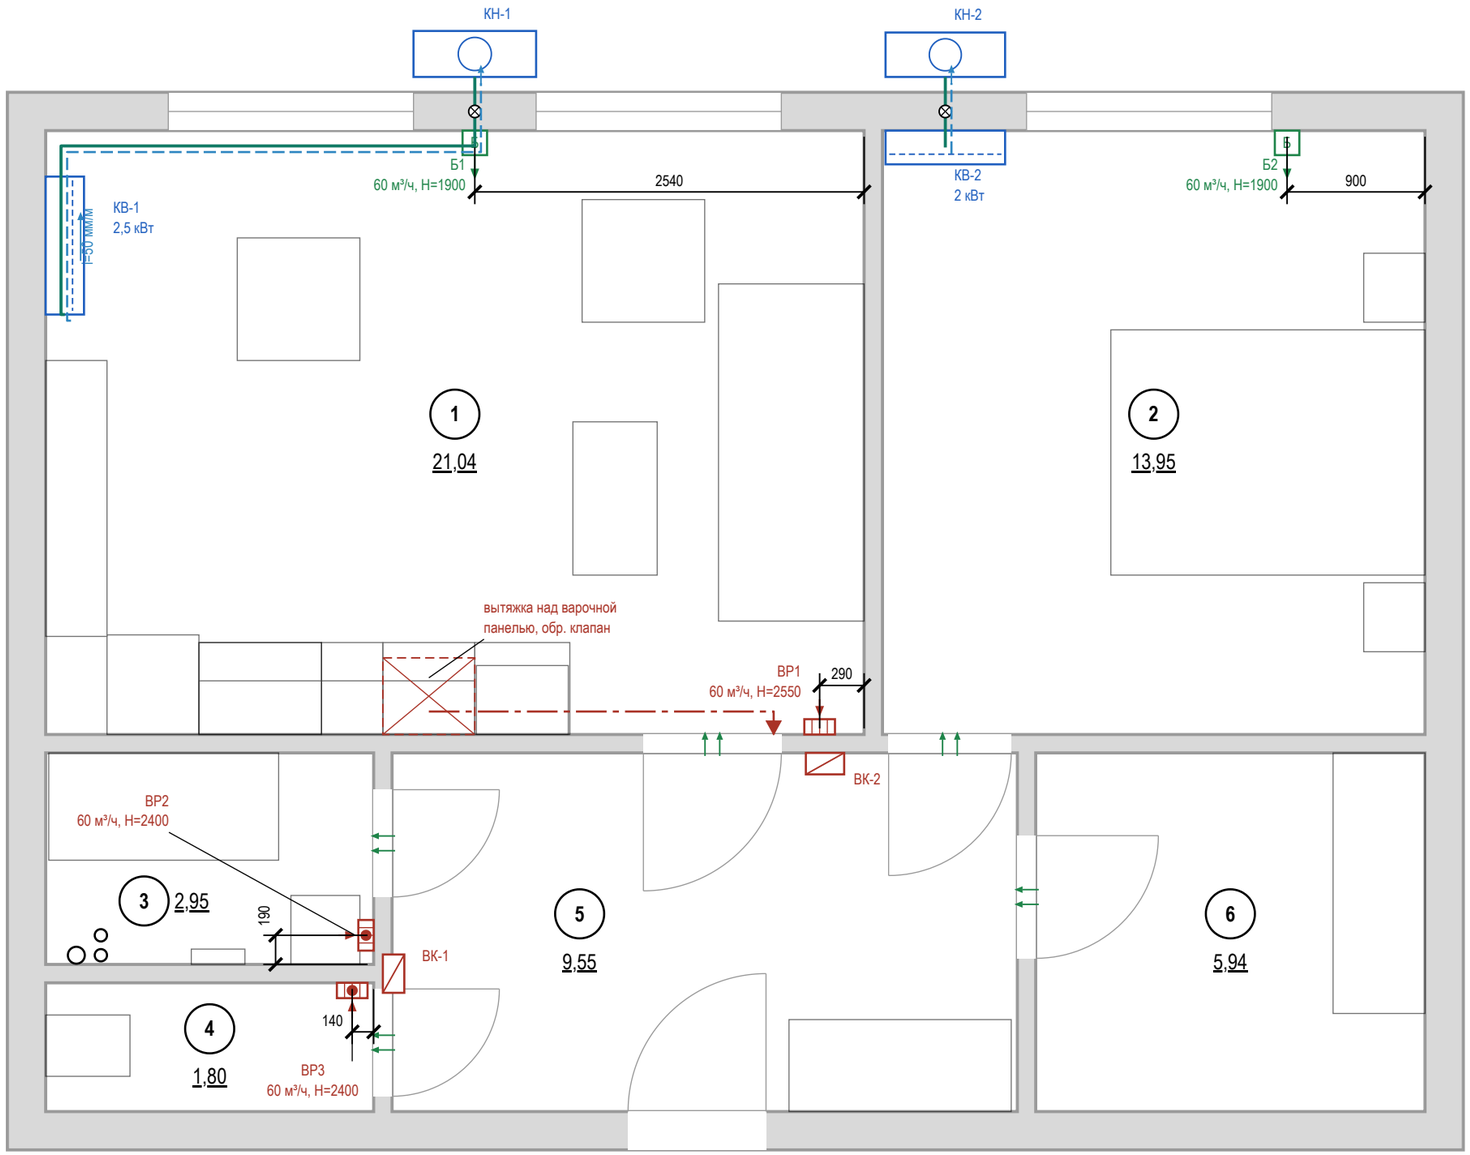

Примечания

1. Расчёт систем ОВ и подбор оборудования — проектная организация с допуском СРО; лист даёт места, трассы и привязки.
2. Нормы вытяжки — СП 54.13330.2022 (Изм. 1, 2), табл. 7.1: кухня с электроплитой 60 м³/ч, с газовой 100; ванная и совмещённый санузел 50; уборная 25; гардеробная 0,2 ч⁻¹. Приток в жилые — 3 м³/ч на 1 м² (менее 20 м² общей площади на человека), иначе 30 м³/ч на человека.
3. Вентканалы и шахты не сужать, не переносить и не закрывать; вентилятор и кухонная вытяжка — через обратный клапан, без перекрытия естественной тяги.
4. Кухонная вытяжка в воздухообмен не включена: воздуховод не менее Ø125 в коробе, вход в канал отдельный.
5. Переток — зазор под полотнами межкомнатных дверей или переточная решётка.
6. Дренаж кондиционера — непрерывный уклон 40–60 мм/м без контруклонов (СТО НОСТРОЙ 2.23.1-2011, п. 5.8.4); врезка в К1 — через сифон (п. 5.8.9); длина трассы и перепад высот — по паспорту блока; внутренний блок — не ближе 150 мм к потолку, не над кроватью и рабочим местом.
7. Наружный блок на фасаде многоквартирного дома — с согласия собственников (общее имущество); при наличии корзин — только в них.
8. «п» в графе «Трасса» — трасса фреона по плану короче минимума, разница выбрана компенсационной петлёй (бухтой): КВ-2 — по плану 0,8 м, с петлёй 3,0 м. Длина петли принята по минимуму трассы (3,0 м) и зависит от паспорта модели кондиционера, которая ещё не выбрана: минимум и максимум трассы — типовые, по паспорту модели, до заказа сверить и при необходимости изменить петлю или место наружного блока. Бухту уложить в коробе или за внутренним блоком, не в штробе.
9. Привязки оборудования — по паспортам приобретённых моделей, до черновых работ.

Условные обозначения

- стояк: К1 — канализация, В1 — ХВС, Т3 — ГВС
- 1 — номер помещения, площадь м²
- вытяжная решётка в вентканал: марка, расход м³/ч, Н центра от чистого пола
- вытяжная решётка с бытовым вентилятором и обратным клапаном: марка, расход, Н
- Б — бризер (приток с фильтром и подогревом)
- переток: зазор под полотном или переточная решётка
- кухонная вытяжка над варочной панелью
- Вентканал ВК-N.
- воздуховод кухонной вытяжки в коробе под потолком
- отдельный вход воздуховода в вентканал, обратный клапан
- внутренний блок кондиционера (КВ-N)
- наружный блок (КН-N) на фасаде / в корзине
- трасса фреонопровода и межблочного кабеля
- дренаж конденсата (уклон стрелкой)
- отверстие в наружной стене под трассу

Воздухообмен, м³/ч

№	Помещение	Выт. норма	Выт. проект	Прит. норма	Прит. проект	Устрой-ства
1	Кухня-гостиная	60	60	60	60	ВР1, Б1
2	Спальня			60	60	Б2
3	Ванная	50	60			ВР2
4	Санузел	25	60			ВР3
6	Гардеробная	3				переток
	Итого	**138**	**180**	**120**	**120**	
	Норма по жильцам: 30×2			60		

Воздухообмен квартиры — по большей из сумм притока и вытяжки: норма 138 м³/ч, проект 180 м³/ч.
Вытяжка не меньше притока — баланс сведён.

Кондиционеры

Марка	Помещение	Нар. блок	Трасса, м	Дренаж
КВ-1	1. Кухня-гостиная	КН-1	3,0	наружу, i=50 мм/м
КВ-2	2. Спальня	КН-2	3,0 п	наружу, i=50 мм/м

Привязки — до обмера
Вентканалы ВК-N приняты проектировщиком, решётки и воздуховоды — от них. До черновых работ — обмер каналов и тяги, лист перевыпустить по факту.

	Лист	№ док.	Подпись	Дата
Дизайнер	Кырлан А.С.			14.11.26
Проверил				
Н. контр.				
Утв.				


Проект: Квартира 58 м² — **М 1:40**

План вентиляции

Стадия	Лист	Листов
П	49	92

выпуск 14.11.2026 № 2b6bd7c078 · стр. 49 из 92

План отопления (М 1:40)

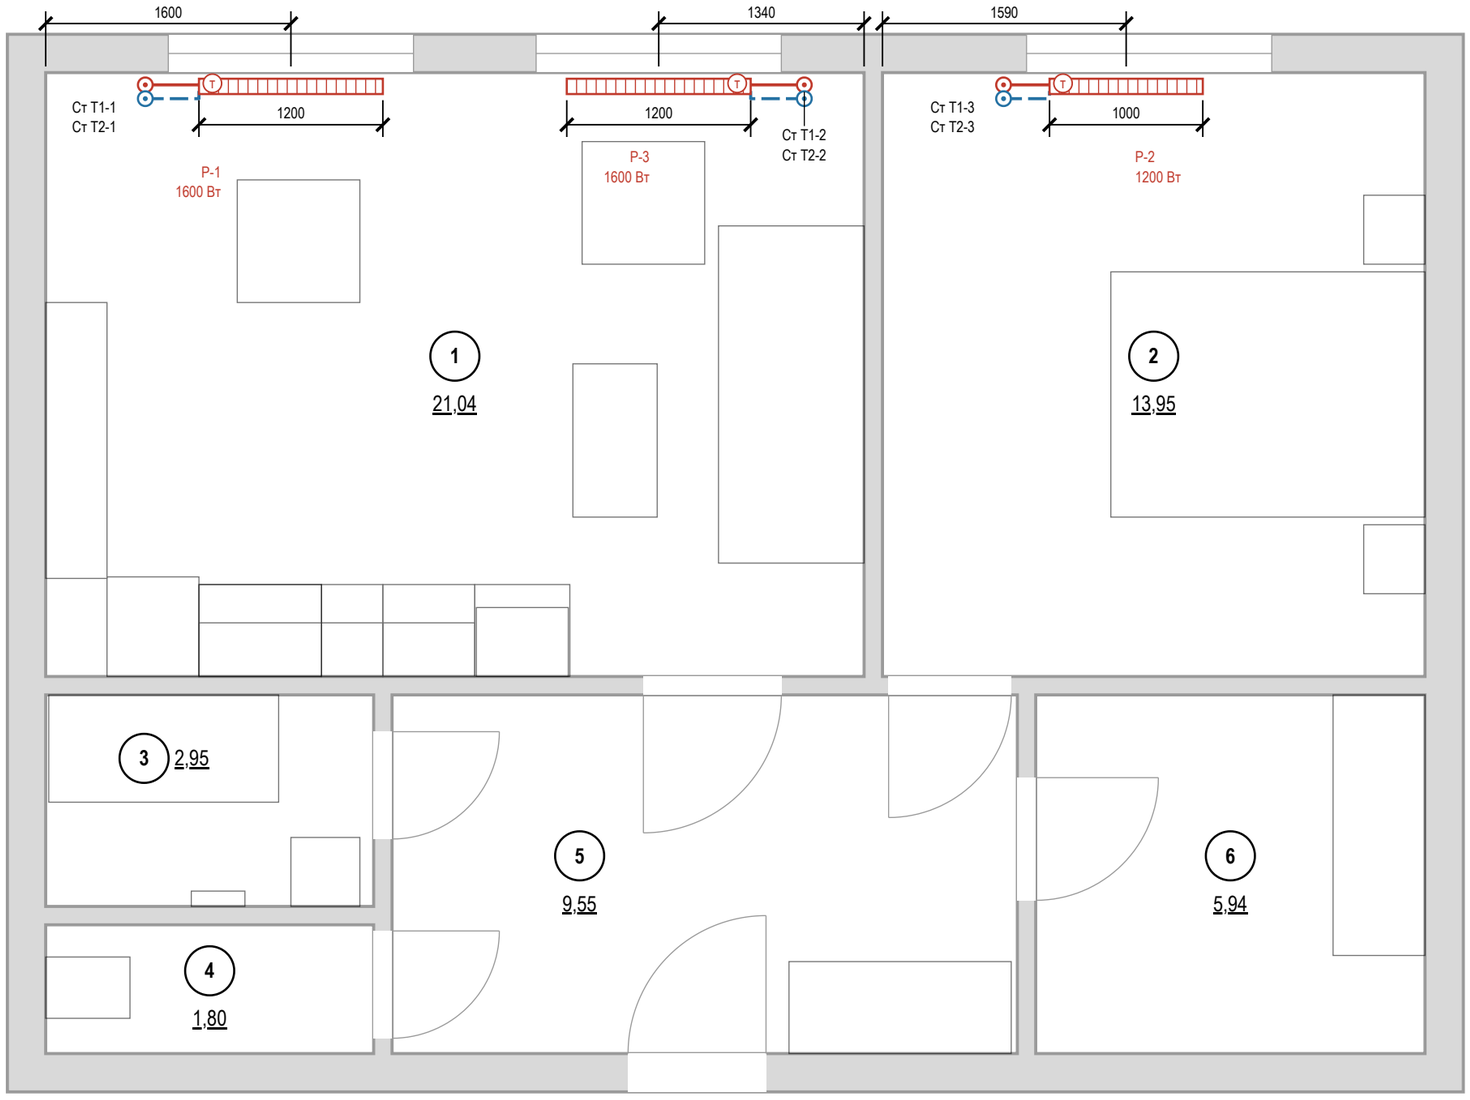

Условные обозначения

- 1 — номер помещения, площадь м²
- радиатор отопления (марка РО-N, длина по плану)
- Т — клапан с термоголовкой на подаче
- стояк отопления, подающий (Ст Т1-N)
- стояк отопления, обратный (Ст Т2-N)
- Т1 — отопление, подающий трубопровод
- Т2 — отопление, обратный трубопровод

Ведомость радиаторов

Марка	Помещение	Тип	Д×В×Г, мм	Низ / стена	Q, Вт
Р-1	1. Кухня-гостиная	панельный 22	1200×500×100	120 / 40	1600
Р-3	1. Кухня-гостиная	панельный 22	1200×500×100	120 / 40	1600
Р-2	2. Спальня	панельный 22	1000×500×100	120 / 40	1200


Низ — от чистого пола, стена — зазор до задней панели, мм.

Привязки — до обмера
Стояки отопления в исходных данных не заданы: показаны у откосов окон, подводки — принципиально. До черновых работ — обмер стояков и паспорта приборов; лист перевыпустить по факту.




Примечания

1. Расчёт системы отопления, теплопотерь и подбор приборов — проектная организация с допуском СРО; лист даёт места и привязки.
2. Тип, длина и мощность радиаторов — по теплотехническому расчёту; лист задаёт места, зазоры и подключение.
3. Зазоры радиатора: низ не менее 100 мм от чистого пола, верх не менее 100 мм до подоконника, 30–50 мм от стены до задней панели; центр по оси окна с допуском ±20 мм. Верх до подоконника — 180 мм.
4. Радиаторы не закрывать глухими коробами и мебелью; перенос и замена приборов в многоквартирном доме — переустройство, согласование с управляющей организацией (ЖК РФ ст. 25–26); вынос на лоджию запрещён.
5. Трубы отопления через межквартирные стены не прокладывать (СП 51.13330.2011, п. 9.19); через перекрытия и перегородки — в гильзах.
6. Привязки приборов и подводок — по паспортам приобретённых радиаторов и клапанов, до черновых работ.
7. До закрытия отделкой трубопроводы отопления испытать гидростатическим давлением с оформлением акта (СП 73.13330.2016, 7.2–7.3).

	Лист	№ док.	Подпись	Дата	Проект: Квартира 58 м²	М 1:40
Дизайнер	Кырлан А.С.			14.11.26		
Проверил					План отопления	Стадия: П; Лист: 50; Листов: 92
Н. контр.						
Утв.						

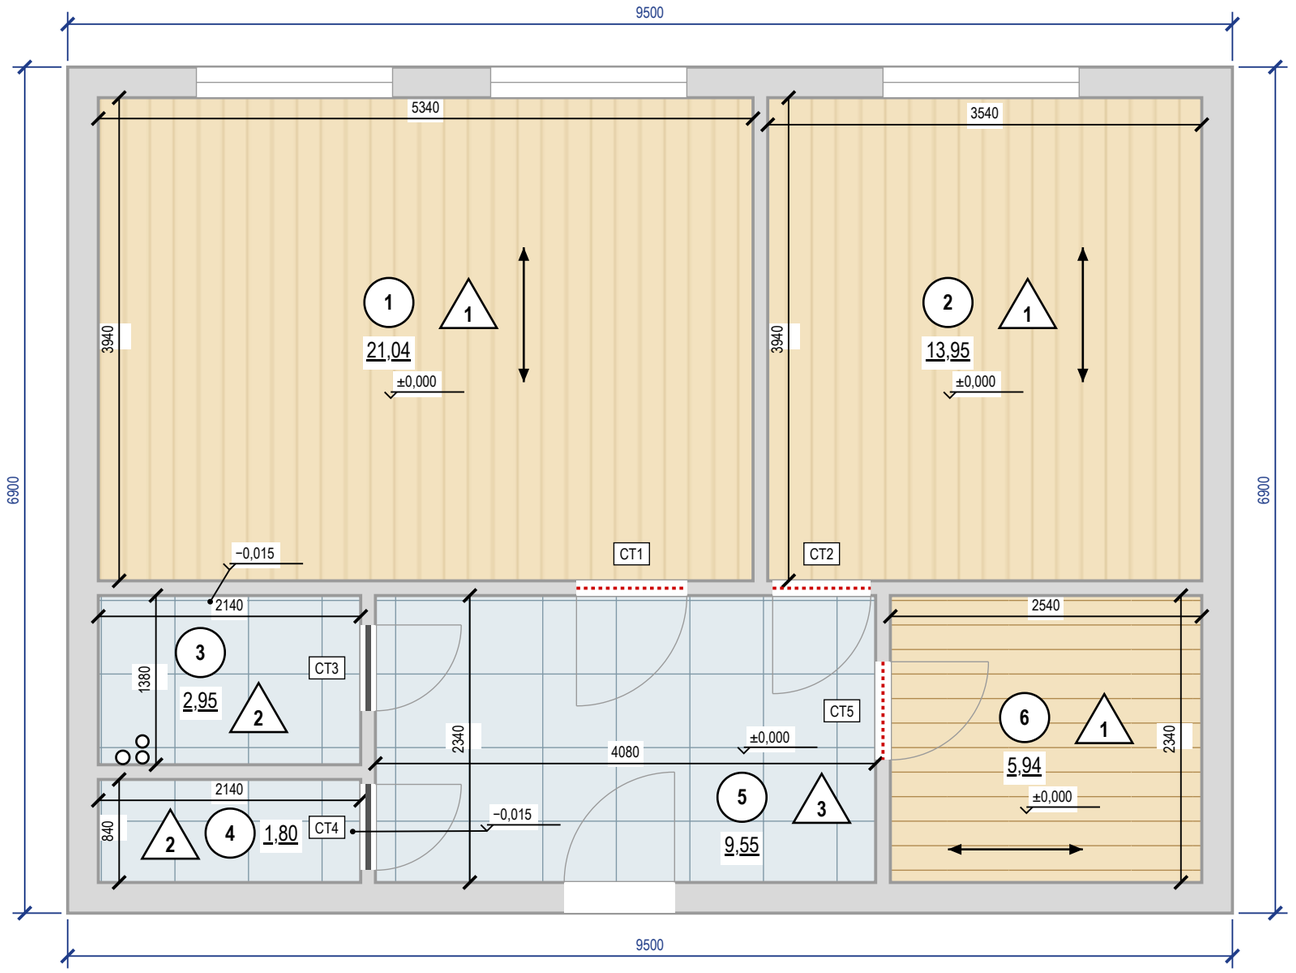

Экспликация полов

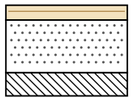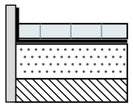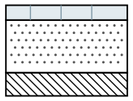Номер помещения	Тип пола	Схема пола	Данные элементов пола (наименование, толщина, основание), мм	Площадь, м²
1, 2, 6	1		Инженерная доска на клею — 14 Стяжка ЦПС М200 — 50 Плита перекрытия Всего 64 мм; ЧП ±0,000, верх плиты −0,064	40,93
3, 4	2		Керамогранит на клею С2 TE S1 — 14 Гидроизоляция обмазочная, 2 слоя, с заведением на стены 200 мм — 2 Стяжка ЦПС М200 — 33 Плита перекрытия Всего 49 мм; ЧП −0,015, верх плиты −0,064	4,75
5	3		Керамогранит на клею С2 TE S1 — 14 Стяжка ЦПС М200 — 50 Плита перекрытия Всего 64 мм; ЧП ±0,000, верх плиты −0,064	9,55
			Итого	**55,23**

Раскладка покрытий

Пом.	Укладка	Старт (оси от чистовых стен), мм	Отступ 1-го ряда / крайние плитки, мм
1	вдоль стен Б/Г, прямая	от стены Г, 1-й ряд вдоль неё	зазор от стены не задан
2	вдоль стен Б/Г, прямая	от стены Г, 1-й ряд вдоль неё	зазор от стены не задан
3	плитка	раскладка плиточника не задана	
4	плитка	раскладка плиточника не задана	
5	плитка	раскладка плиточника не задана	
6	вдоль стен А/В, прямая	от стены А, 1-й ряд вдоль неё	зазор от стены не задан

Спецификация плинтусов

Наименование	Помещения	Длина, м (с запасом)
SX184, h = 110 мм, крепление к стене, окраска в цвет NCS S 0300-N	1, 2, 5	44
SX184, h = 110 мм, крепление к стене, окраска в цвет Tikkurila V503	6	10

Примечания

1. За отметку ±0,000 принят чистый пол, не существующий (блок отметок). Площади — по чистым размерам помещений, м²; размеры — в мм.
2. Стык разнотипных покрытий — по оси дверного полотна (под полотном в закрытом положении); решение стыка — по ведомости стыков.
3. Пол санузлов ниже смежных помещений на 15 мм за счёт меньшей толщины стяжки (верх плиты общий — по экспликации полов); гидроизоляция по стяжке с заведением на стены не менее 200 мм (СП 29.13330.2011, п. 7.2), до облицовки — тест проливом и акт скрытых работ.
4. Трубопроводы в конструкции пола не прокладываются: пирог пола 49–64 мм не вмещает выпуски канализации с уклоном — выпуски К1 ведутся по стенам над чистым полом в коробах (лист 26).
5. Звукоизоляционный слой под стяжкой проектом не предусмотрен (стяжка по плите): приведённый уровень ударного шума перекрытия с полом Lnw не более 60 дБ (СП 51.13330.2011, табл. 2) подтвердить по данным дома; при превышении — плавающая стяжка по звукоизоляции с демпферной лентой по контуру и у стояков, пирог пересчитать.
6. Штучные покрытия (инженерная доска): направление — по стрелке; влажность основания по СМ не более 2,0 % (по ТУ изготовителя).
7. Ровность основания — просвет под 2-метровой рейкой не более 2 мм: пом. 1, 2, 6 (инженерная доска), пом. 3, 4, 5 (керамогранит); проверить до укладки покрытия (СП 71.13330.2017, табл. 8.5).
8. Сетка на плитке — условная, в размер формата; точка старта и раскладка — по листу раскладки плитки.
9. Узор покрытия (заливка-код типа пола) прерывается под надписями — площадями помещений и отметками чистого пола.
10. Пироги полов — по экспликации полов: слои сверху вниз, толщины в мм; гидроизоляция мокрых зон — в пироге и в ведомости отделки; схема пола — без масштаба.

Отметки по высоте

±0,000 чистый пол пом. 1, 2, 5, 6; отсчёт высот
−0,015 чистый пол пом. 3, 4, ниже на 15 мм
−0,064 верх плиты — расчёт, не замер (задание на обмер)
сущ. пол снимается до плиты; не замерен (задание на обмер)

	Лист	№ док.	Подпись	Дата
Дизайнер	Кырлан А.С.			14.11.26
Проверил				
Н. контр.				
Утв.				


Проект: Квартира 58 м² — **М 1:50**

План покрытий пола


Стадия	Лист	Листов
П	51	92

выпуск 14.11.2026 № 2b6bd7c078 · стр. 51 из 92

Фрагмент 1. Ванная (пом. 3). Пол 600×600, шов 2 мм (М 1:20)

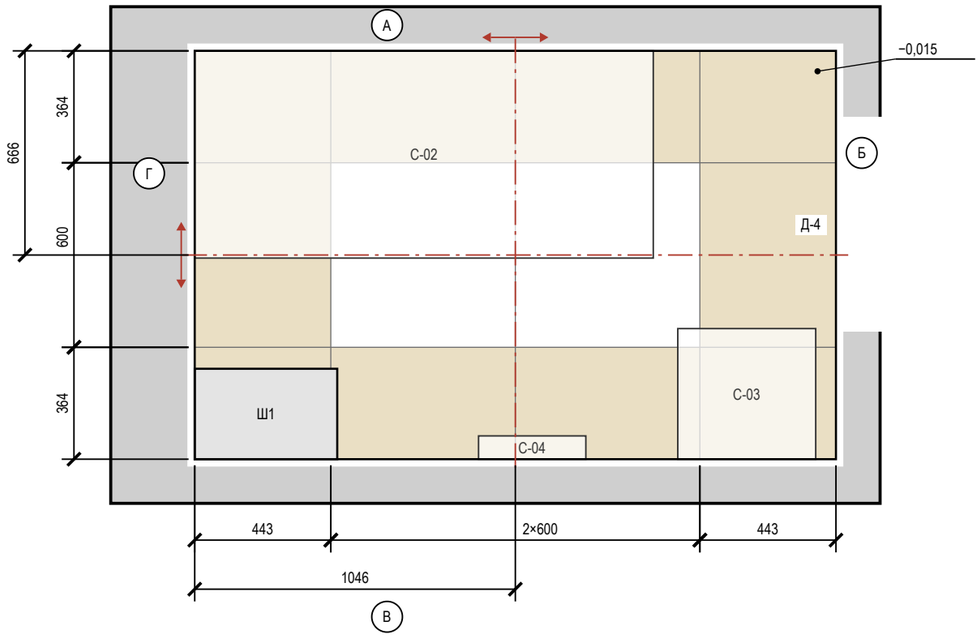

Фрагмент 2. Санузел (пом. 4). Пол 600×600, шов 2 мм (М 1:20)

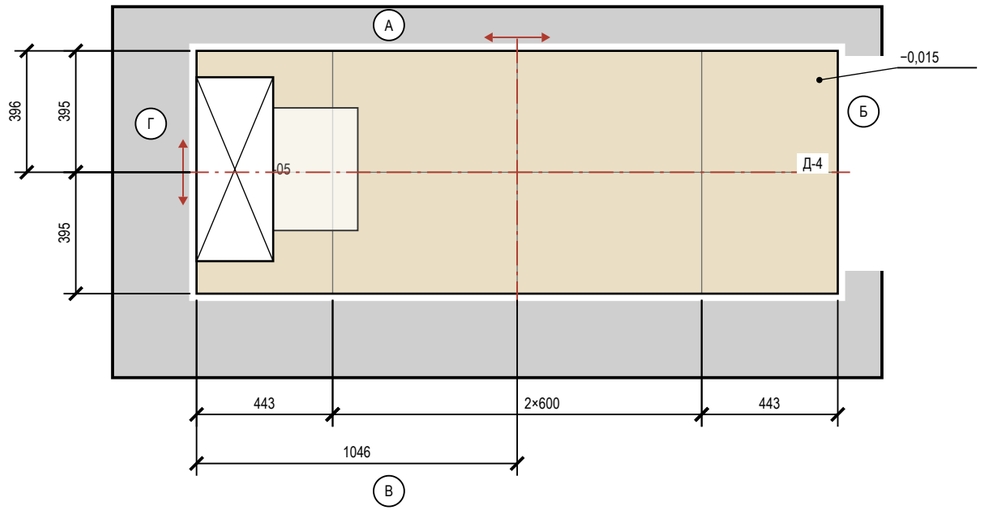

Ведомость материалов

Материал	Класс, код	Норма расхода	Кол-во
Затирка	класс не задан	(a+b)/ab·шов·t·1,6	3,9 кг
Клей	С2 S1	1,2 кг/м²·мм, слой 5	28 кг (2 меш.)
Клей	С2	1,2 кг/м²·мм, слой 5	266 кг (11 меш.)
Гидроизоляция	обмазочная, 2 слоя: пол, стены по периметру и зоны замачивания	по ТУ	13,4 м²
Демпф. лента	по периметру пола из плитки		21,0 м

Ведомость плитки

Помещение, поверхность	Плитка, код	Формат	Шов	S, м²	Целых	Подр.	С запасом
Ванная, пол	SG651622R	600×600	2	2,95	2	10	14
Ванная, стены А–Г	610015000370	1200×600	2	14,95	0	40	44
Ванная, короб стояков Ш1 489×319	610015000370	1200×600	2	1,99	0	10	12
Санузел, пол	SG651622R	600×600	2	1,80	0	8	9
Санузел, стены А–Г	610015000370	1200×600	2	13,40	0	30	34
Санузел, короб инсталляции	610015000370	1200×600	2	1,47	0	7	8
Прихожая, пол	SG651622R	600×600	2	9,55	10	18	31
Итого 600×600				14,30	12	36	54
Итого 600×1200				**31,80**	**0**	**87**	**98**

Условные обозначения

- плитка целая; тонкая линия — шов
- плитка с подрезкой (размер — на цепочке)
- ось старта; стрелки — направление укладки
- сантехприбор: габарит, высота по практике
- короб инсталляции: плитка пола — до короба
- короб стояков (Ш…): плитка пола — до короба
- отметка чистого пола на полке выноски, м
- (А) обозначение стены А–Г (как на развёртках)


Примечания

1. Раскладка от чистовых размеров: стены санузлов теряют 10 + 5 + 9 = 24 мм на сторону (штукатурка, клей, плитка); подрезки — чистые, без шва.
2. Старт — от центра помещения (штрихпунктир, стрелки — направление укладки); размер старта — от чистовых стен Г и А.
3. Раскладка пола «Прихожая» — на листе «Раскладка плитки. Прихожая».
4. Калибр партии не задан — до укладки замерить (рабочий размер W, ГОСТ 13996-2019) и пересчитать подрезки.
5. Количество: целые по раскладке + по одной на подрезку, запас 10 %; один артикул — одна партия и тон. Исключены поддон, короб, проёмы и места за коробом; S — по чистым граням: стены нетто = зона облицовки по ведомости отделки − место за коробом инсталляции 2,71 м² (плитку за коробом не кладут), короб — отдельной строкой.
6. Клей С2 S1; С2 (ГОСТ Р 56387-2018), затирка класс не задан; расход — по ТУ выбранной марки.
7. Гидроизоляция: пол и стены 200 мм от ЧП; над ванной — до 2000 и 300 мм за борт (пом. 3) (см. развёртки); акт скрытых работ, пролив 24 ч.
8. Отметка чистого пола −0,015, порог 15 мм; стык с соседним покрытием — по оси полотна двери.

	Лист	№ док.	Подпись	Дата	Проект: Квартира 58 м²			М 1:20
Дизайнер	Кырлан А.С.			14.11.26	Раскладка плитки. Планы полов	Стадия	Лист	Листов
Проверил						П	52	92
Н. контр.								
Утв.								

выпуск 14.11.2026 № 2b6bd7c078 · стр. 52 из 92

Фрагмент 1. Прихожая (пом. 5). Пол 600×600, шов 2 мм (М 1:20)

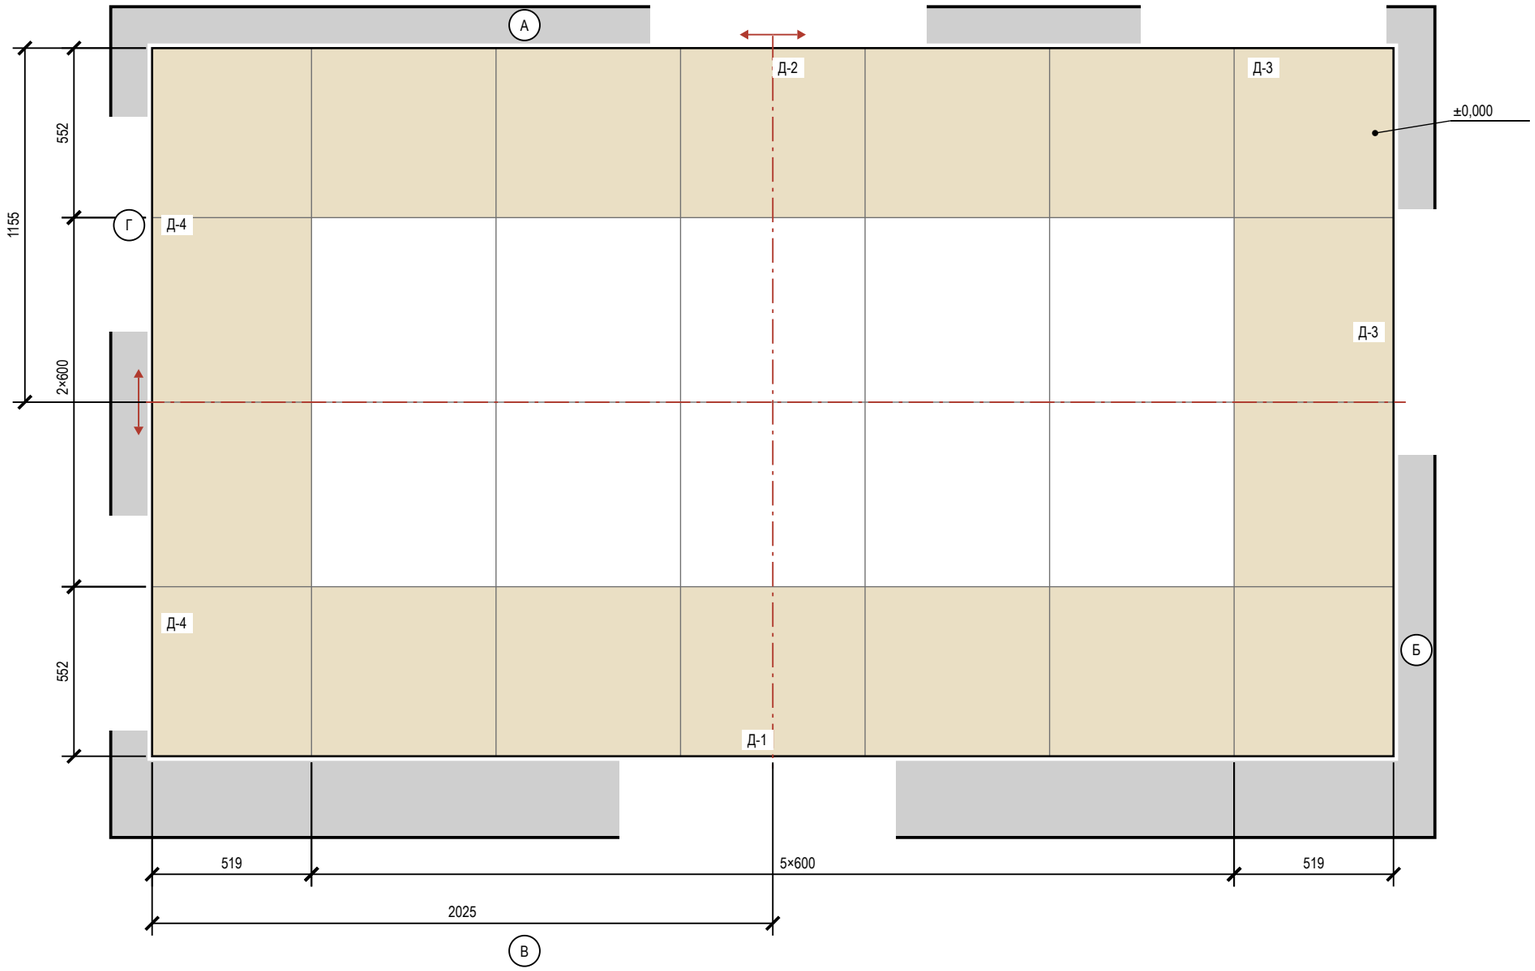

Условные обозначения

- плитка целая; тонкая линия — шов
- плитка с подрезкой (размер — на цепочке)
- ось старта; стрелки — направление укладки
- отметка чистого пола на полке выноски, м
- (А) обозначение стены А–Г (как на развёртках)

Подсчёт плитки

Поверхность	Формат	S, м²	Целых	Подр.	С запасом
Прихожая, пол	600×600	9,55	10	18	31

Примечания

1. Прихожая: керамогранит 600×600, длинная сторона — вдоль стен Б и Г, шов 2 мм, прямая раскладка от центра. Стены окрашены: раскладка от чистового контура минус штукатурка и шпаклёвка 15 мм на сторону (принято); подрезки 519 / 552 мм, срез — под плинтус.
2. Прихожая: деформационный зазор по периметру 8–10 мм под плинтусом; в проёмах — стык с соседним покрытием по оси полотна двери. Клей С2, затирка класс не задан.
3. Клей, затирка и итог по форматам — в ведомостях листа «Раскладка плитки. Планы полов».

	Лист	№ док.	Подпись	Дата
Дизайнер	Кырлан А.С.			14.11.26
Проверил				
Н. контр.				
Утв.				

Проект: Квартира 58 м² — **М 1:20**

Раскладка плитки. Прихожая

Стадия	Лист	Листов
П	53	92

Стена В (М 1:25)


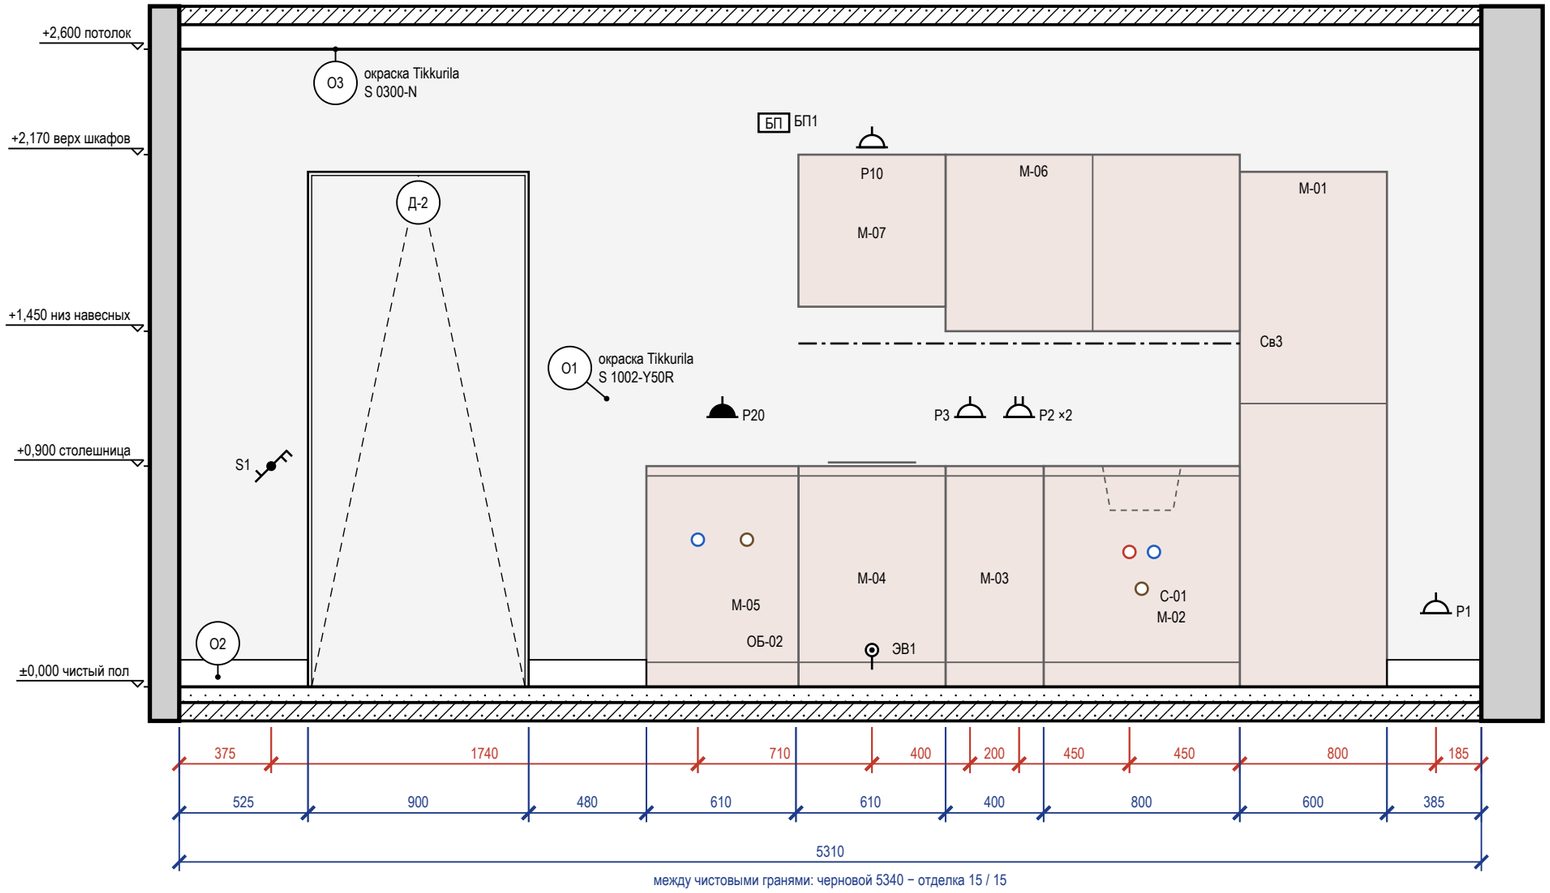


Схема развёрток (М 1:100)

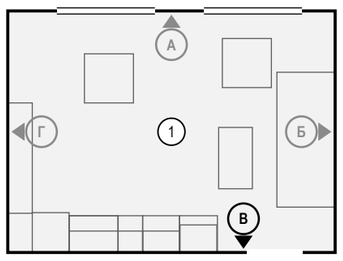

Ведомость изделий и проёмов (на листе)

Марка	Изделие, проём	На виде Ш×В, мм	Низ, мм
Д-2	дверь скрытого монтажа	900×2100	0
М-05	ниша под стиральную машину под столешницей, фасад на петлях	620×900	0
ОБ-02	стиральная машина узкая 600 × 450, фронтальная загрузка	600×850	0
М-04	модуль нижний	600×900	0
М-07	навесной модуль над варочной, вытяжка встраивается в дно	600×620	1550
М-03	модуль нижний	400×900	0
М-06	модуль навесной	1200×720	1450
С-01	мойка кухонная	800×900	0
М-02	модуль нижний	800×900	0
М-01	пенал кухонный	600×2100	0


Примечания

1. Размеры — в мм от чистовых поверхностей стен; условные обозначения и общие указания — лист 12.
2. Двери скрытого монтажа — полотно в плоскости стены, отделка стены по полотну, плинтус прерывается у короба (узел — на листе узлов).
3. Выводы кухонной техники — по утверждённому проекту кухни: привязки выводов даются от осей модулей гарнитура.
4. Потолок — у каждой стены свой, по плану потолков (ПТ2); ступени — зоной, кромка короба перед нишей — тонкой линией; в поле потолка: ПТ1 +2,550.
5. Часть марок не уместилась у знаков: коды, высоты и привязки этих позиций — в ведомости точек и выводов под видами.

Ведомость точек и выводов

Марка	Что это	Гр.	Н, мм	От угла, мм	Примечание
S1	выключатель	1	900	375	
В1-2	холодная вода — стиральная машина		600	2115	кран машины
Р20	розетка: стиральная машина	6	1100	2215	IP44
К1-2	канализация — стиральная машина		600	2315	Ø40
БП1	блок питания LED	1	2300	2425	
ЭВ1	вывод кабеля: варочная панель	3	150	2825	
Р10	розетка: вытяжка (встроена в дно М-07)	2	2200	2825	
Р3	розетка: рабочая зона	2	1100	3225	
Р2	розетка: рабочая зона	2	1100	3425	рамка 2 поста
Т3-1	горячая вода — мойка кухонная		550	3875	межос. 100
К1-1	канализация — мойка кухонная		400	3925	Ø50
В1-1	холодная вода — мойка кухонная		550	3975	межос. 100
Св3	светильник настенный	1	1400	4325	лента 2525–4325 от угла
Р1	розетка: холодильник	2	300	5125	

Стена В — визуализация, лист 4

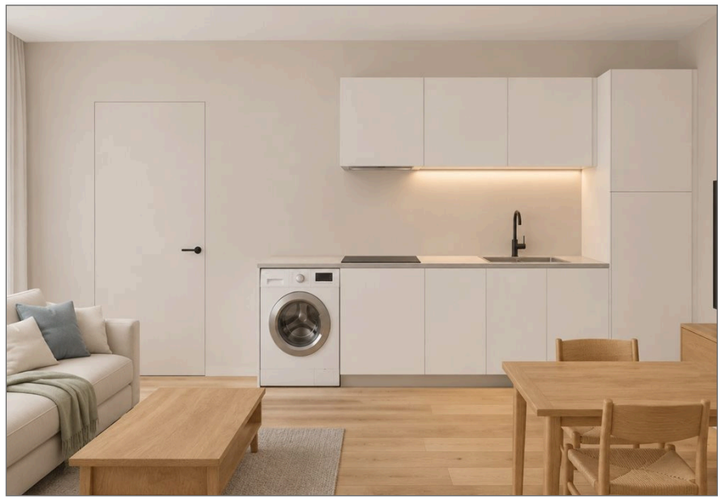

Ведомость отделки (на листе)

Марка	Поверхность	Материал, изделие	Цвет, код	Кол.
О1	стены	окраска, Tikkurila, шелковисто-матовая, подготовка Q3	NCS S 1002-Y50R	11,9 м²
О2	плинтус	плинтус МДФ, Orac Decor Luxxus, h 110 мм, SX184, шелковисто-матовая	NCS S 0300-N	1,4 м
О3	потолок	окраска, Tikkurila, глубокоматовая	NCS S 0300-N	21 м²

	Лист	№ док.	Подпись	Дата
Дизайнер	Кырлан А.С.			14.11.26
Проверил				
Н. контр.				
Утв.				

Проект: Квартира 58 м² — М 1:25

Развёртка стены В. Кухня-гостиная (пом. 1), кухонный фронт

Стадия	Лист	Листов
П	54	92

выпуск 14.11.2026 № 2b6bd7c078 · стр. 54 из 92

Стена А (М 1:20)


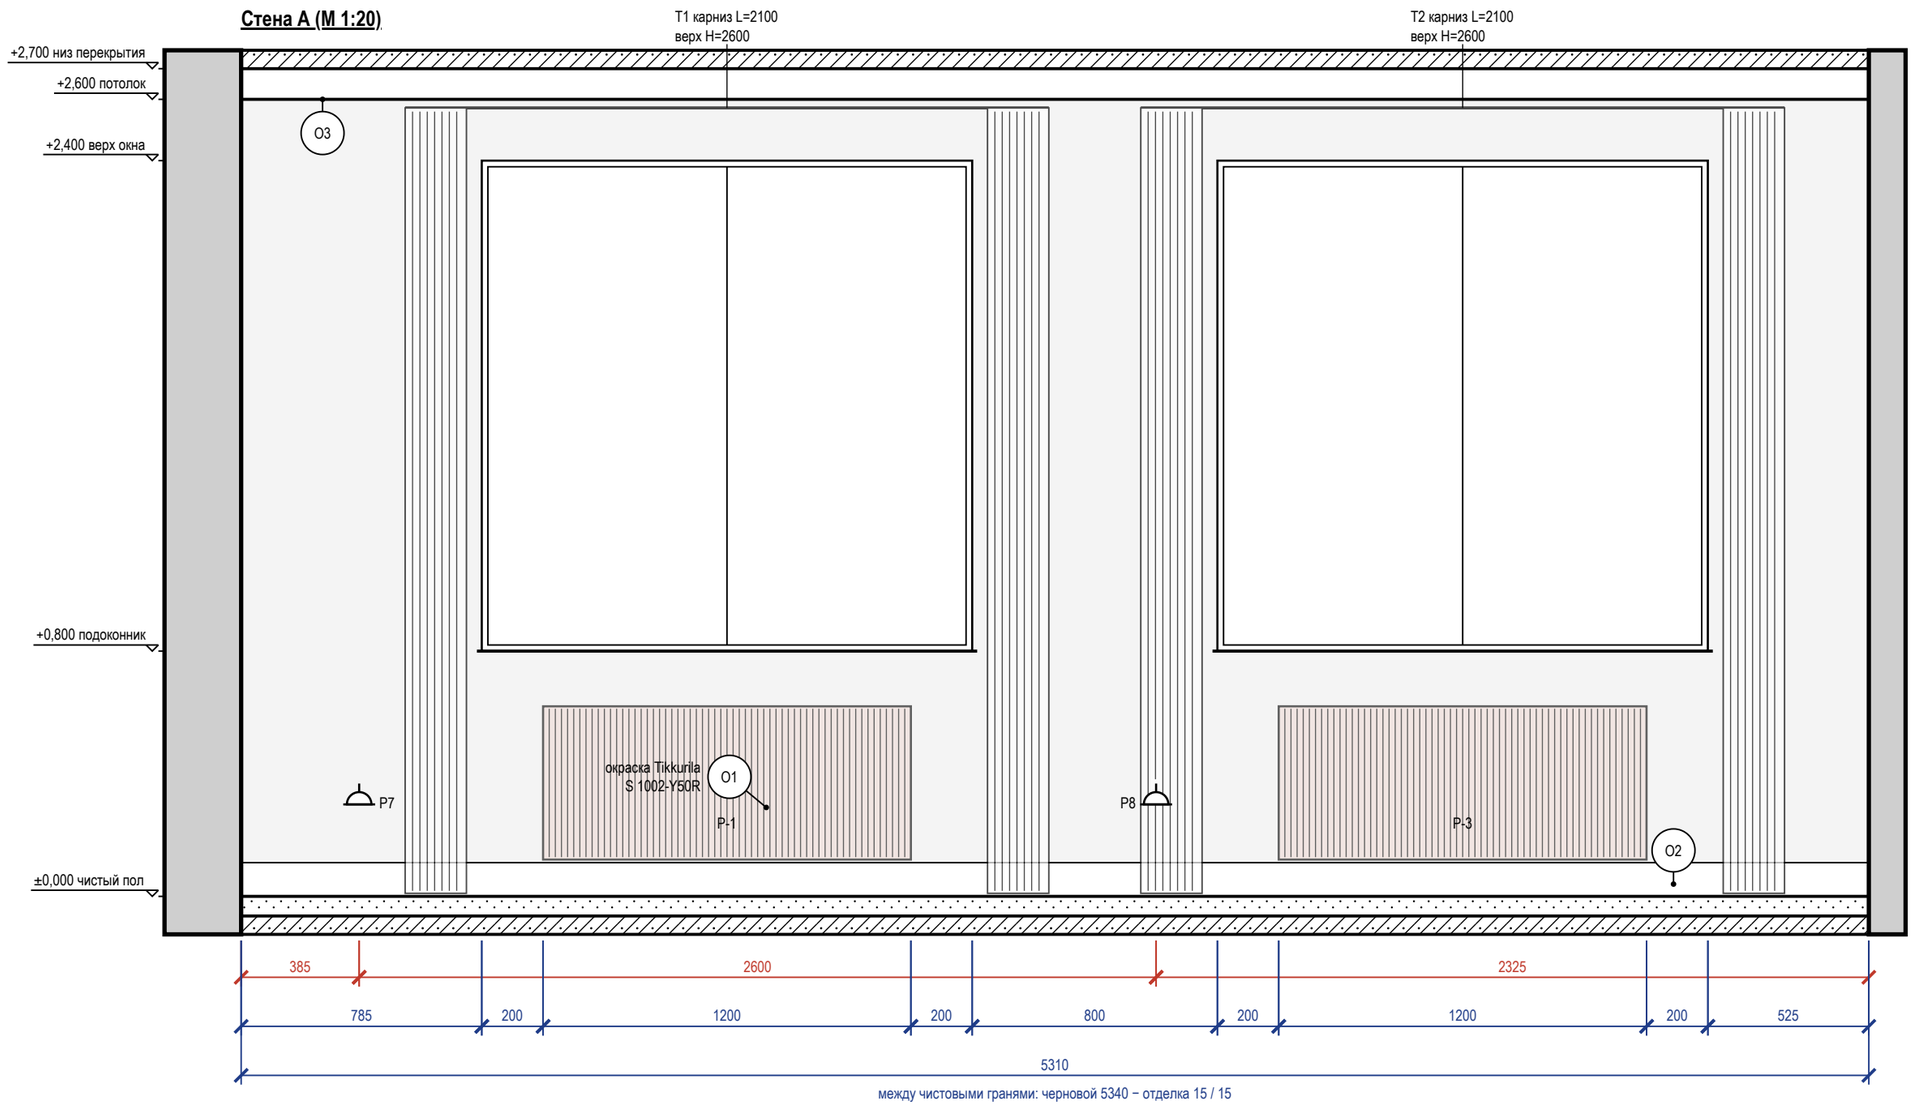


Схема развёрток (М 1:100)

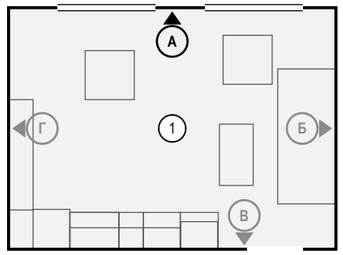

Ведомость точек и выводов

Марка	Что это	Гр.	Н, мм	От угла, мм	Примечание
P7	розетка: торшер	4	300	385	
P8	розетка: зона отдыха	4	300	2985	

Ведомость отделки (на листе)

Марка	Поверхность	Материал, изделие	Цвет, код	Кол.
O1	стены	окраска, Tikkurila, шелковисто-матовая, подготовка Q3	NCS S 1002-Y50R	8,7 м²
O2	плинтус	плинтус МДФ, Orac Decor Luxxus, h 110 мм, SX184, шелковисто-матовая	NCS S 0300-N	5,3 м
O3	потолок	окраска, Tikkurila, глубокоматовая	NCS S 0300-N	21 м²

Ведомость изделий и проёмов (на листе)

Марка	Изделие, проём	На виде Ш×В, мм	Низ, мм
P-1	радиатор отопления	1200×500	120
P-3	радиатор отопления	1200×500	120

Примечания

1. Размеры — в мм от чистовых поверхностей стен; условные обозначения и общие указания — лист 12.
2. Карнизы (шины) — по ведомости текстиля декоратора: длина L и верх H на развёртке — те же числа, что в ведомости; крепление — до окраски потолка.
3. Потолок — у каждой стены свой, по плану потолков (ПТ2); ступени — зоной, кромка короба перед нишей — тонкой линией; в поле потолка: ПТ1 +2,550.
4. Линии узора (швы плитки, складки штор, рёбра радиаторов) прерываются у знаков и выносок — просвет между линиями не менее 0,7 мм.

	Лист	№ док.	Подпись	Дата
Дизайнер	Кырлан А.С.			14.11.26
Проверил				
Н. контр.				
Утв.				


Проект: Квартира 58 м² — **М 1:20**

Развёртка стены А. Кухня-гостиная (пом. 1)

Стадия	Лист	Листов
П	55	92

выпуск 14.11.2026 № 2b6bd7c078 · стр. 55 из 92

Стена Б (М 1:20)

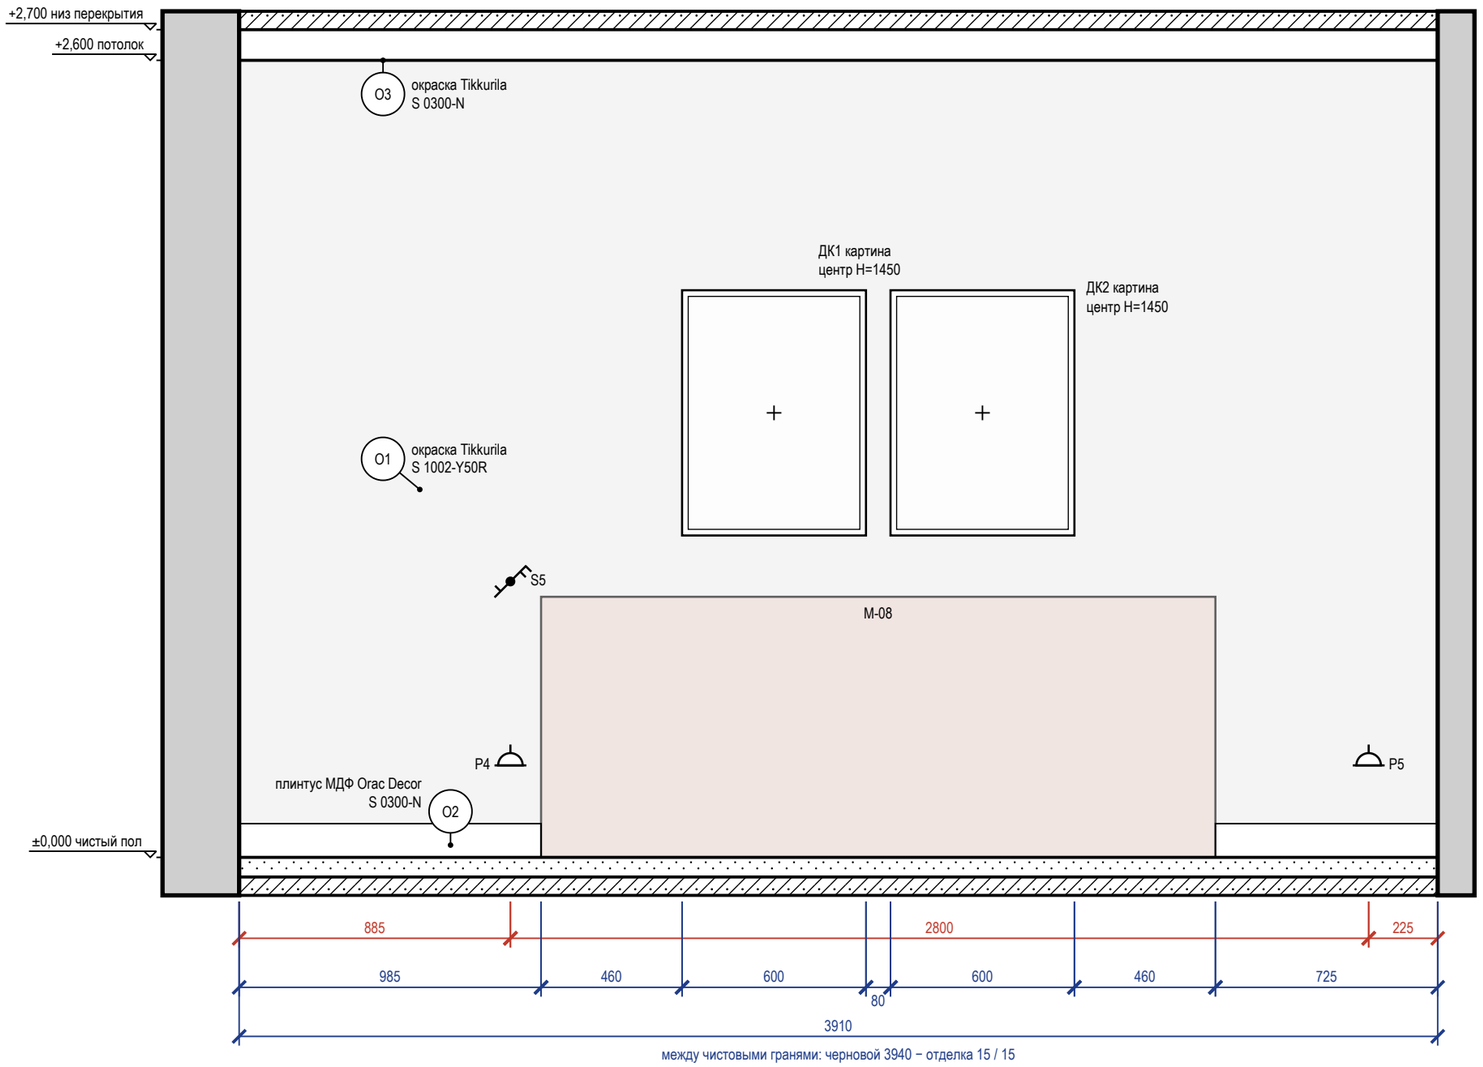


Ведомость точек и выводов

Марка	Что это	Гр.	H, мм	От угла, мм	Примечание
P4	розетка: у дивана	4	300	885	
S5	выключатель	1	900	885	
P5	розетка: у дивана	4	300	3685	

Стена Б — визуализация, лист 3



Схема развёрток (М 1:50)

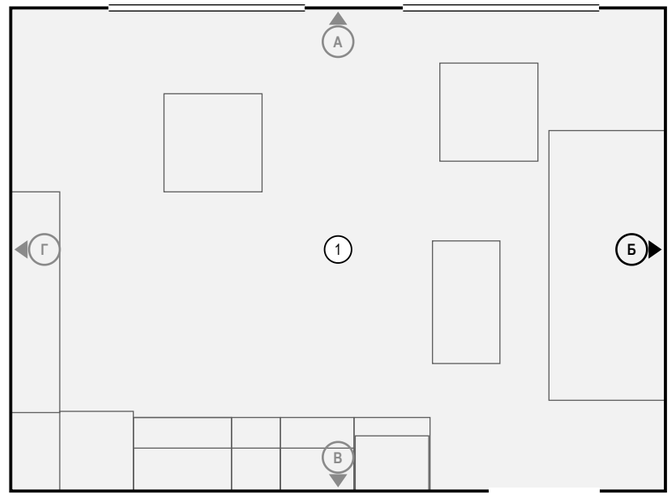

Ведомость отделки (на листе)

Марка	Поверхность	Материал, изделие	Цвет, код	Кол.
О1	стены	окраска, Tikkurila, шелковисто-матовая, подготовка Q3	NCS S 1002-Y50R	10,2 м²
О2	плинтус	плинтус МДФ, Orac Decor Luxxus, h 110 мм, SX184, шелковисто-матовая	NCS S 0300-N	1,7 м
О3	потолок	окраска, Tikkurila, глубокоматовая	NCS S 0300-N	21 м²

Ведомость изделий и проёмов (на листе)

Марка	Изделие, проём	На виде Ш×В, мм	Низ, мм
М-08	диван	2200×850	0
ДК1	картина	600×800	1050
ДК2	картина	600×800	1050

Примечания

1. Размеры — в мм от чистовых поверхностей стен; условные обозначения и общие указания — лист 12.
2. Картины и зеркала крепить к основанию по паспорту изделия (закладные и анкеры — в перечне скрытых работ); крест — ось центра предмета.
3. Потолок — у каждой стены свой, по плану потолков (ПТ2); ступени — зоной, кромка короба перед нишей — тонкой линией; в поле потолка: ПТ1 +2,550.

	Лист	№ док.	Подпись	Дата
Дизайнер	Кырлан А.С.			14.11.26
Проверил				
Н. контр.				
Утв.				


Проект: Квартира 58 м² — **М 1:20**

Развёртка стены Б. Кухня-гостиная (пом. 1)

Стадия	Лист	Листов
П	56	92

выпуск 14.11.2026 № 2b6bd7c078 · стр. 56 из 92

Стена Г (М 1:20)

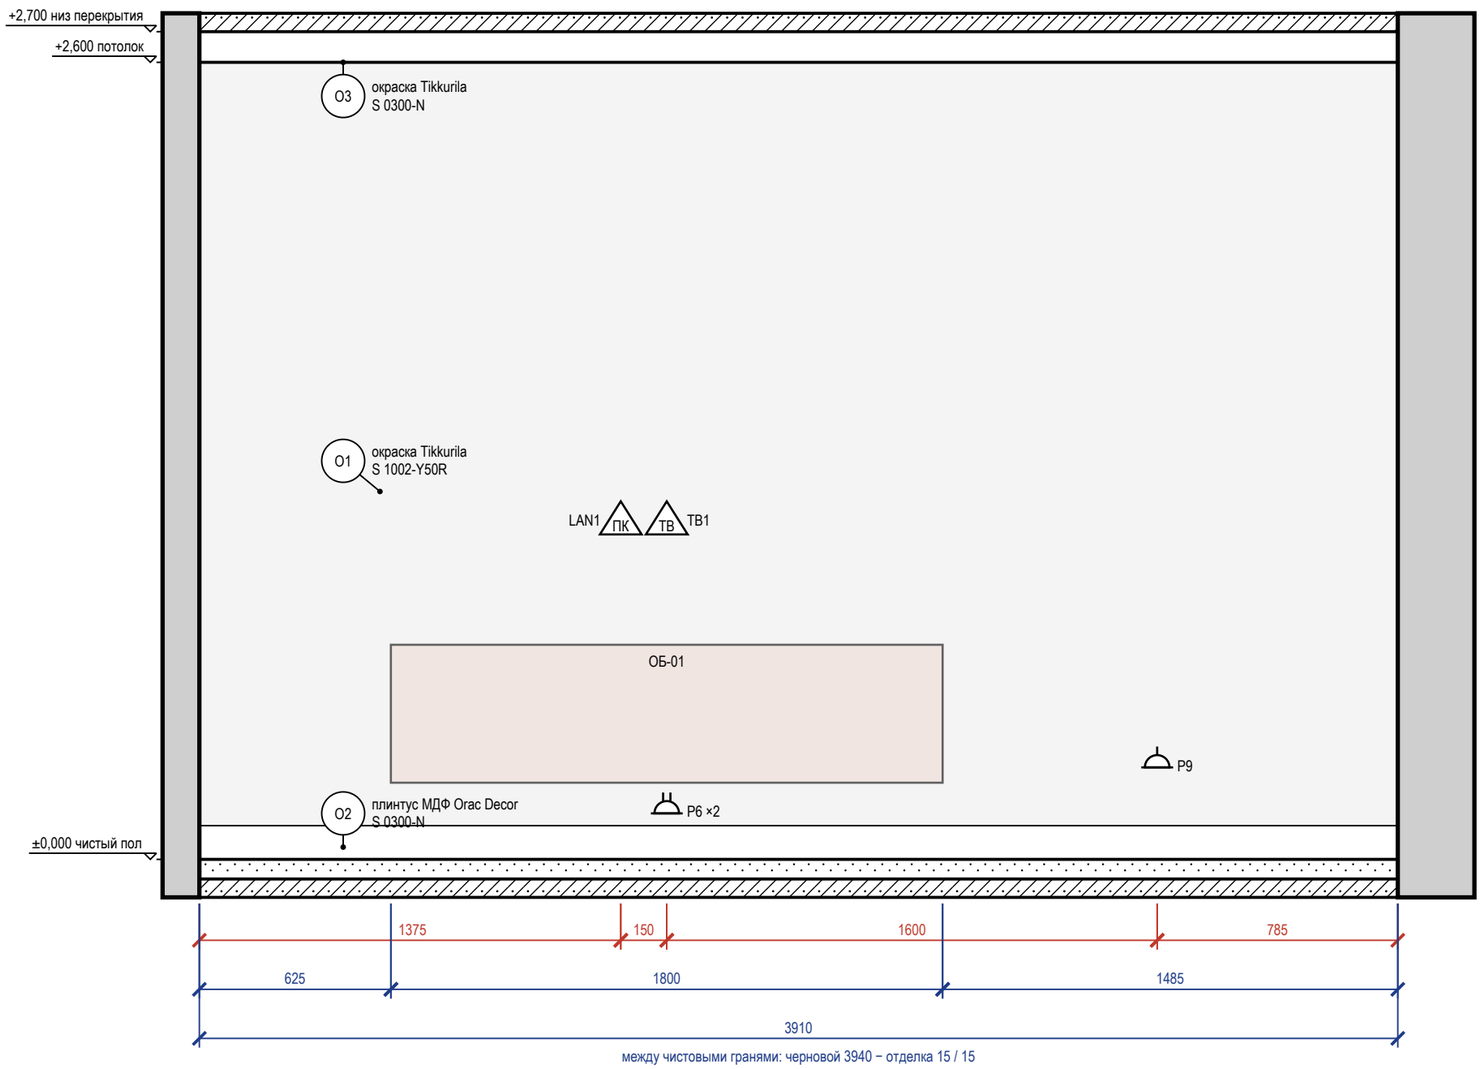


Ведомость точек и выводов

Марка	Что это	Гр.	Н, мм	От угла, мм	Примечание
LAN1	розетка RJ45: ТВ-приставка		1100	1375	
Р6	розетка: ТВ, приставка (за тумбой ОБ-01)	4	150	1525	рамка 2 поста
ТВ1	розетка ТВ: ТВ над тумбой ОБ-01		1100	1525	
Р9	розетка: обеденная зона	4	300	3125	

Стена Г — визуализация, лист 5



Схема развёрток (М 1:50)

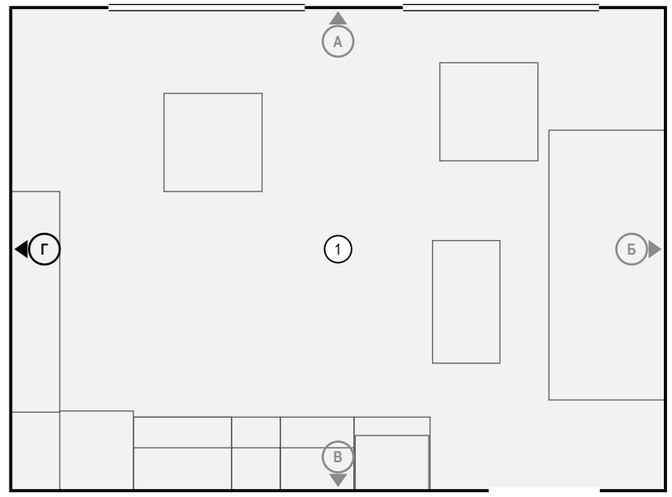

Ведомость отделки (на листе)

Марка	Поверхность	Материал, изделие	Цвет, код	Кол.
О1	стены	окраска, Tikkurila, шелковисто-матовая, подготовка Q3	NCS S 1002-Y50R	10,2 м²
О2	плинтус	плинтус МДФ, Orac Decor Luxxus, h 110 мм, SX184, шелковисто-матовая	NCS S 0300-N	3,9 м
О3	потолок	окраска, Tikkurila, глубокоматовая	NCS S 0300-N	21 м²

Ведомость изделий и проёмов (на листе)

Марка	Изделие, проём	На виде Ш×В, мм	Низ, мм
ОБ-01	ТВ-тумба подвесная с экраном	1800×450	250

Примечания

1. Размеры — в мм от чистовых поверхностей стен; условные обозначения и общие указания — лист 12.
2. Потолок — у каждой стены свой, по плану потолков (ПТ2); ступени — зоной, кромка короба перед нишей — тонкой линией; в поле потолка: ПТ1 +2,550.

	Лист	№ док.	Подпись	Дата
Дизайнер	Кырлан А.С.			14.11.26
Проверил				
Н. контр.				
Утв.				

Проект: Квартира 58 м² — М 1:20

Развёртка стены Г. Кухня-гостиная (пом. 1)

Стадия	Лист	Листов
П	57	92

выпуск 14.11.2026 № 2b6bd7c078 · стр. 57 из 92

Стена А (М 1:20)


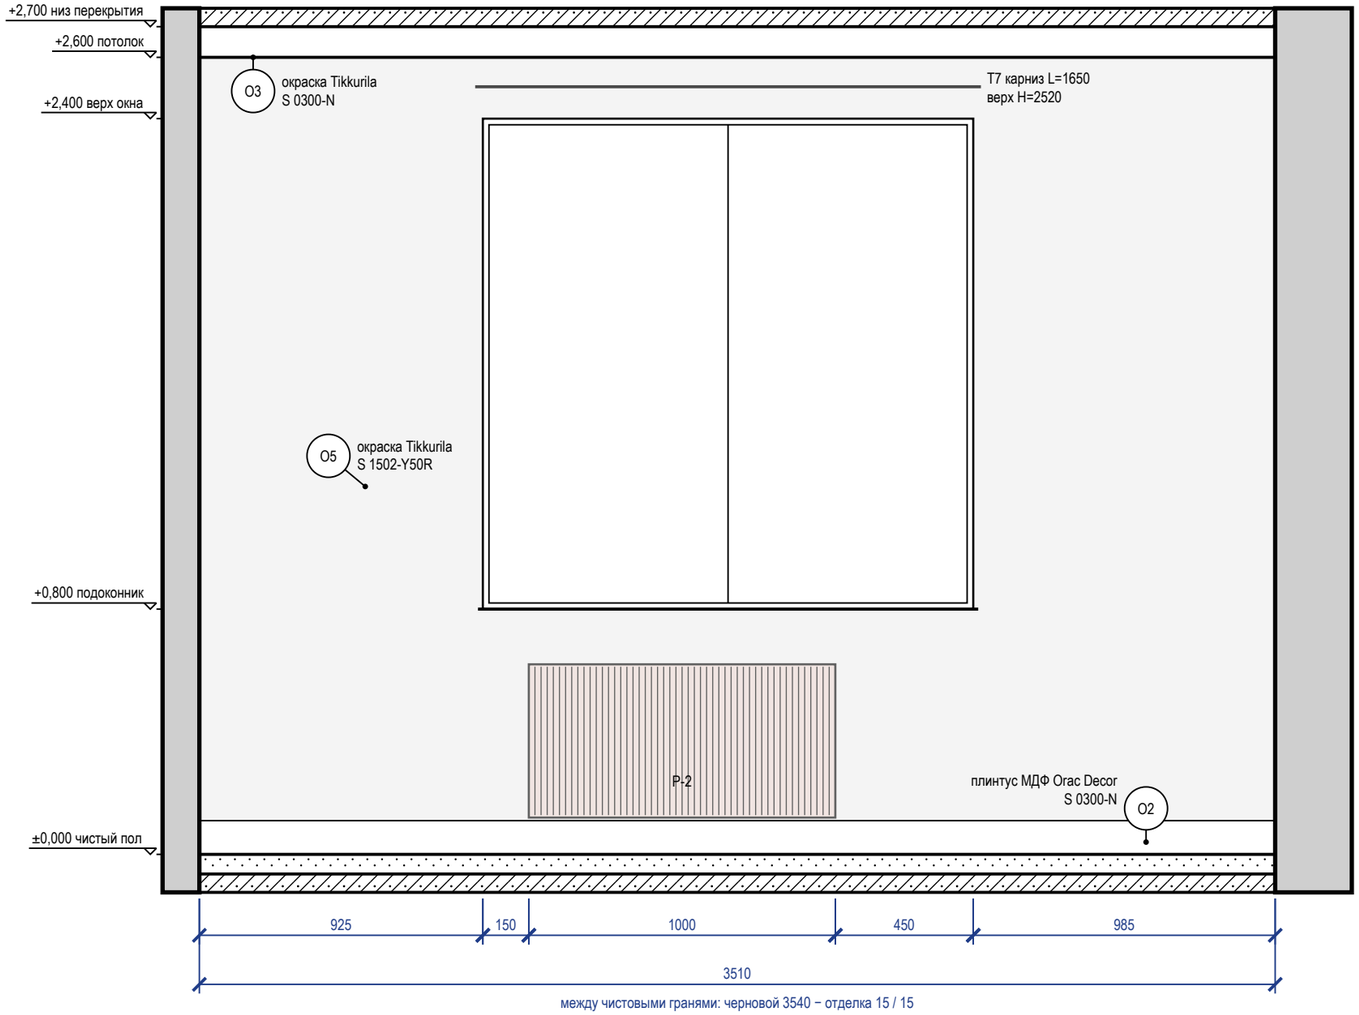


Схема развёрток (М 1:50)

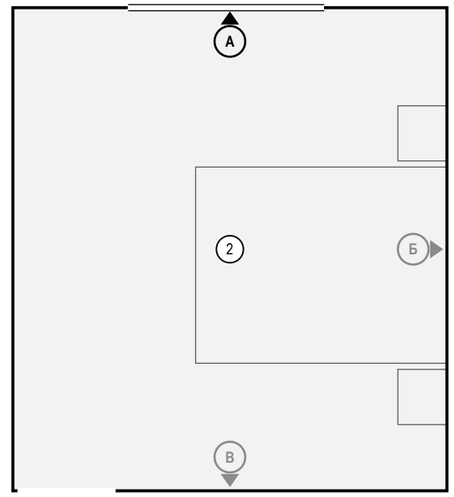

Ведомость отделки (на листе)


Марка	Поверхность	Материал, изделие	Цвет, код	Кол.
О2	плинтус	плинтус МДФ, Orac Decor Luxxus, h 110 мм, SX184, шелковисто-матовая	NCS S 0300-N	3,5 м
О3	потолок	окраска, Tikkurila, глубокоматовая	NCS S 0300-N	13,9 м²
О5	стены	окраска, Tikkurila, глубокоматовая, подготовка Q3	NCS S 1502-Y50R	6,6 м²

Ведомость изделий и проёмов (на листе)

Марка	Изделие, проём	На виде Ш×В, мм	Низ, мм
Р-2	радиатор отопления	1000×500	120

5 **Плинтус МДФ 110×16 мм у окрашенной стены по доске (ламинату) (М 1:10)**

Узел 5 — лист С12

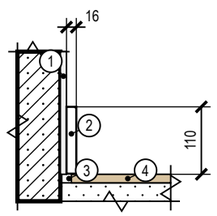

Поз.	Состав слоя, изделие
1	штукатурка, шпаклёвка Q3, окраска — по ведомости отделки
2	плинтус МДФ 110×16 под окраску в цвет стены; клей монтажный — к стене, не к полу
3	зазор покрытия у стены 8–10 мм закрывается плинтусом
4	инженерная доска на клею

Примечания

1. Размеры — в мм от чистовых поверхностей стен; условные обозначения и общие указания — лист 12.
2. Карнизы (шины) — по ведомости текстиля декоратора: длина L и верх H на развёртке — те же числа, что в ведомости; крепление — до окраски потолка.
3. Потолок — у каждой стены свой, по плану потолков (ПТ2); ступени — зоной, кромка короба перед нишей — тонкой линией; в поле потолка: ПТ1 +2,550.

	Лист	№ док.	Подпись	Дата
Дизайнер	Кырлан А.С.			14.11.26
Проверил				
Н. контр.				
Утв.				


Проект: Квартира 58 м² — **М 1:20**

Развёртка стены А. Спальня (пом. 2)

Стадия	Лист	Листов
П	58	92

выпуск 14.11.2026 № 2b6bd7c078 · стр. 58 из 92

Стена Б (М 1:20)

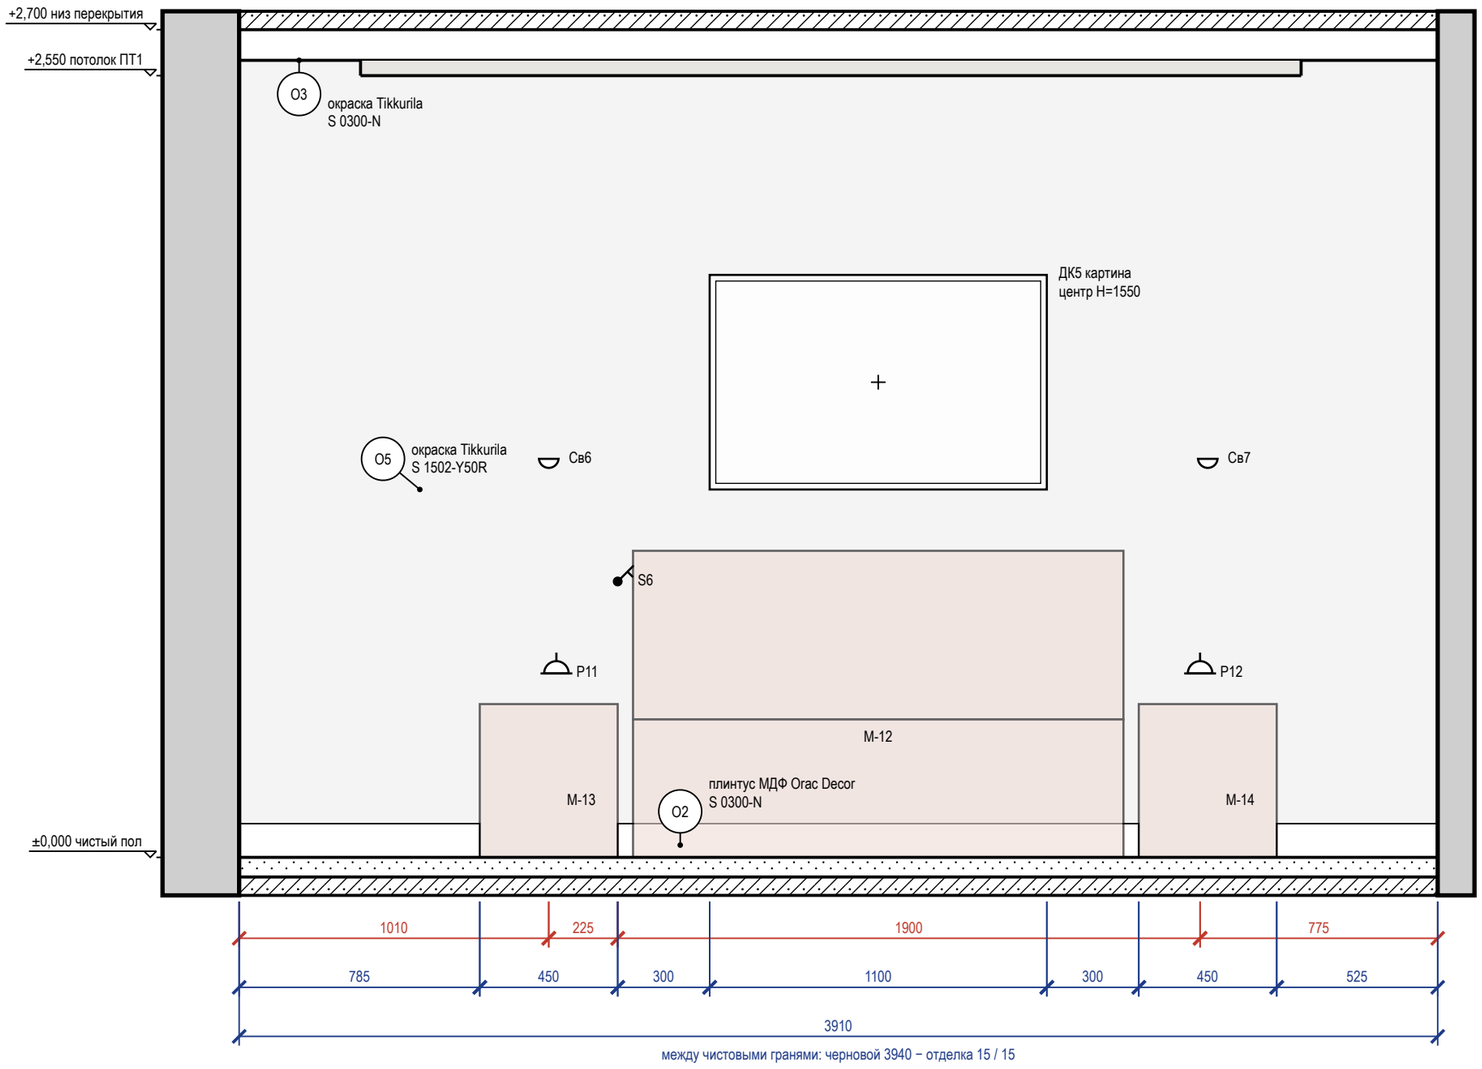

Ведомость точек и выводов

Марка	Что это	Гр.	H, мм	От угла, мм	Примечание
Св6	светильник настенный	1	1300	1010	
P11	розетка	4	600	1035	
S6	выключатель	1	900	1235	
P12	розетка	4	600	3135	
Св7	светильник настенный	1	1300	3160	

Стена Б — визуализация, лист 6


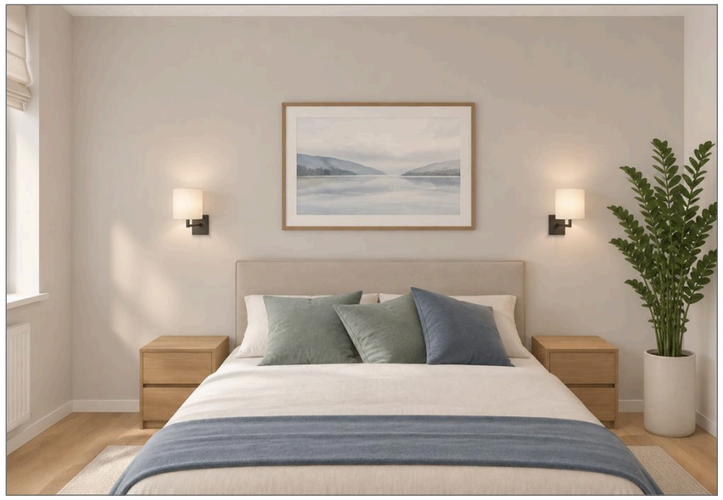


Схема развёрток (М 1:50)

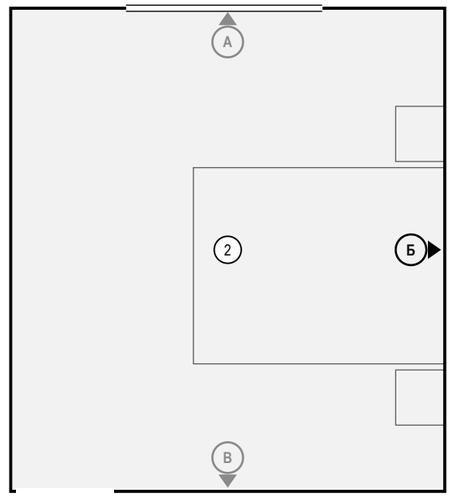

Ведомость отделки (на листе)

Марка	Поверхность	Материал, изделие	Цвет, код	Кол.
О2	плинтус	плинтус МДФ, Orac Decor Luxxus, h 110 мм, SX184, шелковисто-матовая	NCS S 0300-N	3 м
О3	потолок	окраска, Tikkurila, глубокоматовая	NCS S 0300-N	13,9 м²
О5	стены	окраска, Tikkurila, глубокоматовая, подготовка Q3	NCS S 1502-Y50R	10,2 м²

Ведомость изделий и проёмов (на листе)

Марка	Изделие, проём	На виде Ш×В, мм	Низ, мм
М-13	тумба прикроватная	450×500	0
М-12	кровать	1600×450	0
ДК5	картина	1100×700	1200
М-14	тумба прикроватная	450×500	0

Примечания

1. Размеры — в мм от чистовых поверхностей стен; условные обозначения и общие указания — лист 12.
2. Картины и зеркала крепить к основанию по паспорту изделия (закладные и анкеры — в перечне скрытых работ); крест — ось центра предмета.
3. Потолок — у каждой стены свой, по плану потолков (ПТ2, ПТ1); ступени — зоной, кромка короба перед нишей — тонкой линией.

	Лист	№ док.	Подпись	Дата	Проект: Квартира 58 м²			М 1:20
Дизайнер	Кырлан А.С.			14.11.26	Развёртка стены Б. Спальня (пом. 2)	Стадия	Лист	Листов
Проверил						П	59	92
Н. контр.								
Утв.								

выпуск 14.11.2026 № 2b6bd7c078 · стр. 59 из 92

Стена В (М 1:20)


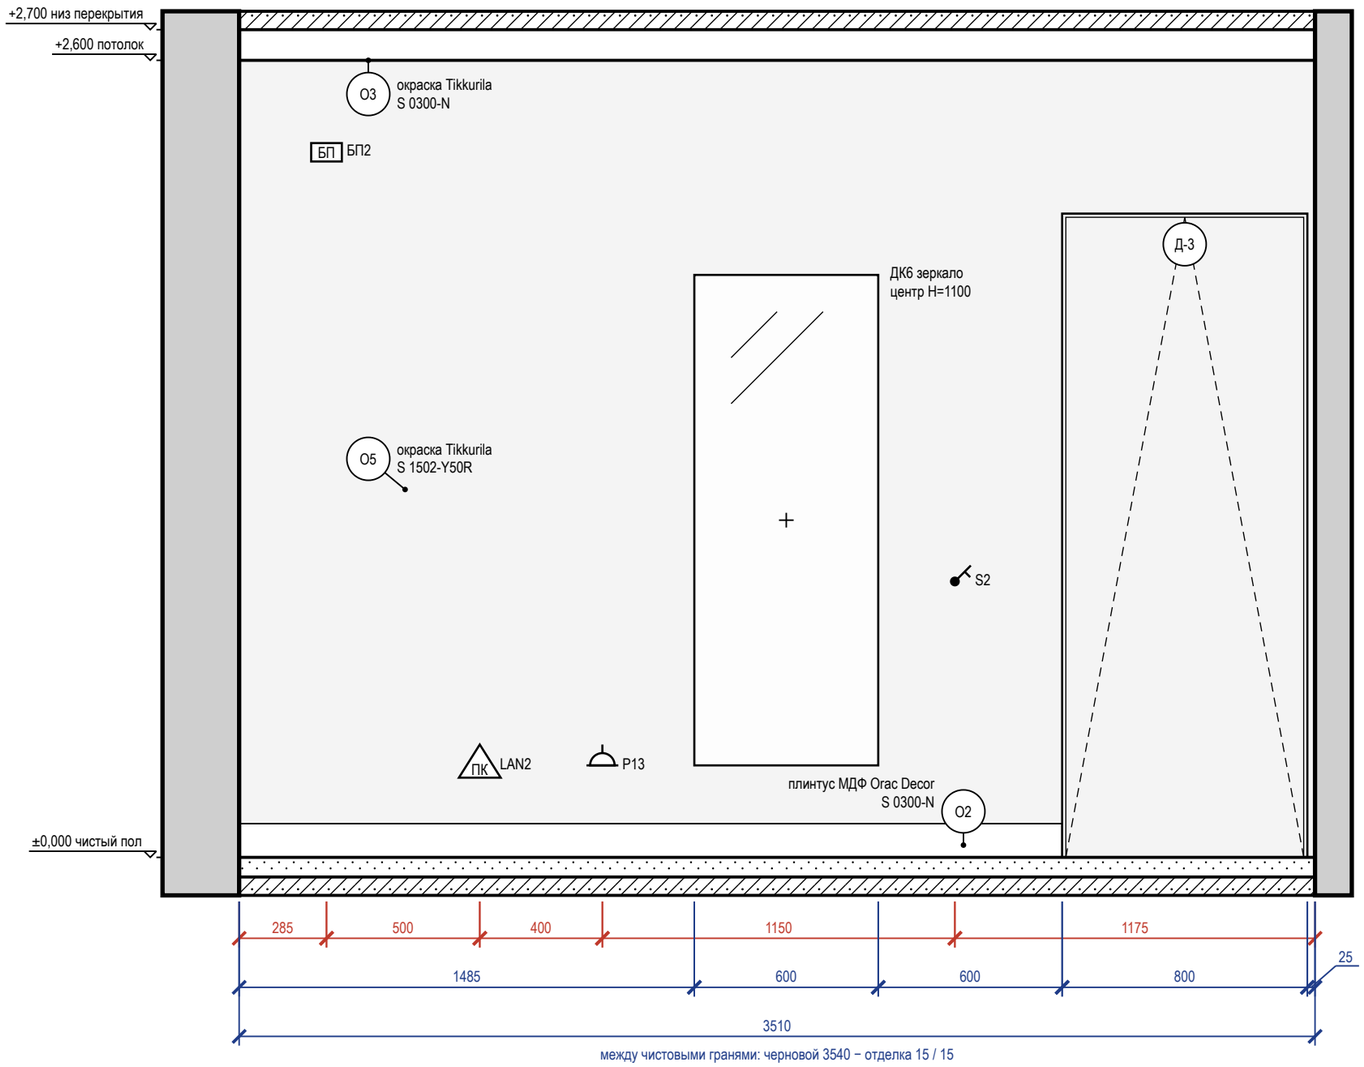


Схема развёрток (М 1:50)

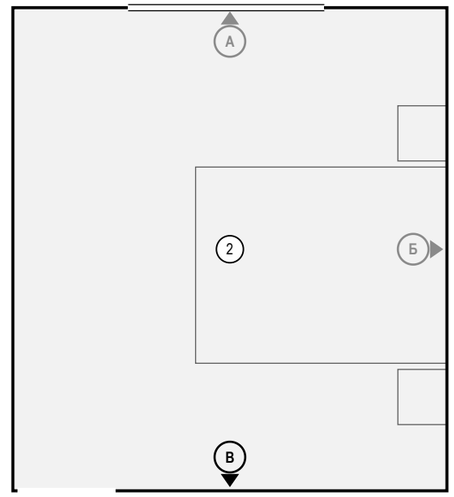

Ведомость точек и выводов

Марка	Что это	Гр.	H, мм	От угла, мм	Примечание
БП2	блок питания LED	1	2300	285	
LAN2	розетка RJ45: рабочее место, ТВ		300	785	
P13	розетка: комод, зарядка	4	300	1185	
S2	выключатель	1	900	2335	

Ведомость отделки (на листе)

Марка	Поверхность	Материал, изделие	Цвет, код	Кол.
О2	плинтус	плинтус МДФ, Orac Decor Luxxus, h 110 мм, SX184, шелковисто-матовая	NCS S 0300-N	2,7 м
О3	потолок	окраска, Tikkurila, глубокоматовая	NCS S 0300-N	13,9 м²
О5	стены	окраска, Tikkurila, глубокоматовая, подготовка Q3	NCS S 1502-Y50R	7,4 м²

Ведомость изделий и проёмов (на листе)

Марка	Изделие, проём	На виде Ш×В, мм	Низ, мм
ДК6	зеркало	600×1600	300
Д-3	дверь скрытого монтажа	800×2100	0

Примечания

1. Размеры — в мм от чистовых поверхностей стен; условные обозначения и общие указания — лист 12.
2. Картины и зеркала крепить к основанию по паспорту изделия (закладные и анкеры — в перечне скрытых работ); крест — ось центра предмета.
3. Двери скрытого монтажа — полотно в плоскости стены, отделка стены по полотну, плинтус прерывается у короба (узел — на листе узлов).
4. Потолок — у каждой стены свой, по плану потолков (ПТ2); ступени — зоной, кромка короба перед нишей — тонкой линией; в поле потолка: ПТ1 +2,550.

	Лист	№ док.	Подпись	Дата
Дизайнер	Кырлан А.С.			14.11.26
Проверил				
Н. контр.				
Утв.				


Проект: Квартира 58 м² — **М 1:20**

Развёртка стены В. Спальня (пом. 2)

Стадия	Лист	Листов
П	60	92


выпуск 14.11.2026 № 2b6bd7c078 · стр. 60 из 92

Стена А (М 1:20)

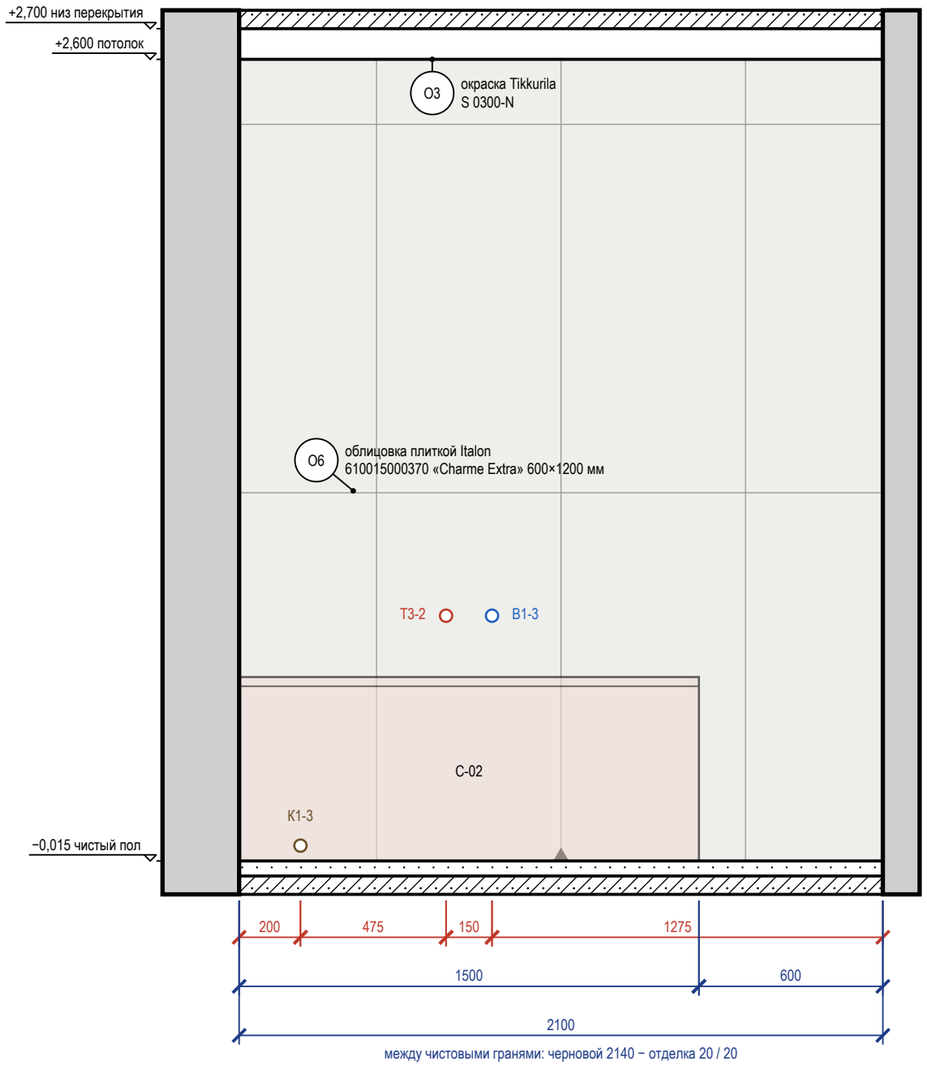

между чистовыми гранями: черновой 2140 − отделка 20 / 20

Стена Б (М 1:20)

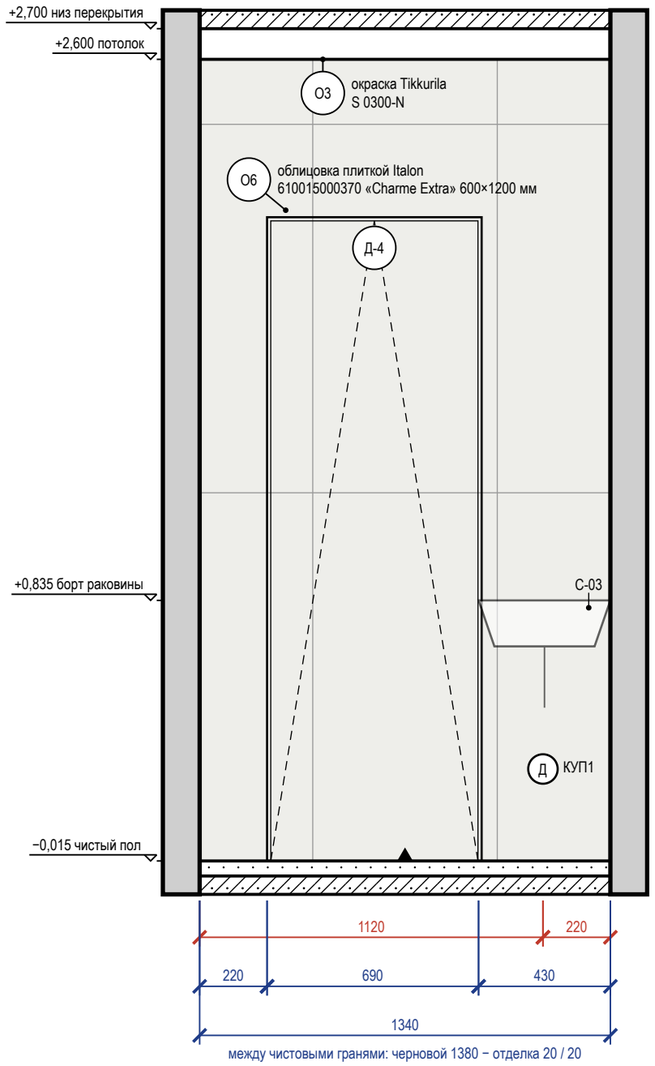


между чистовыми гранями: черновой 1380 − отделка 20 / 20

Стена Б — визуализация, лист 7



Схема развёрток (М 1:50)

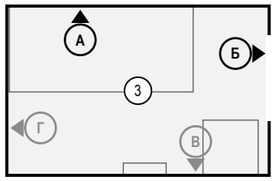

Ведомость точек и выводов

Стена	Марка	Что это	Гр.	Н, мм	От угла, мм	Примечание
А	К1-3	канализация — ванна		50	200	Ø50
А	Т3-2	горячая вода — ванна		800	675	межос. 150
А	В1-3	холодная вода — ванна		800	825	межос. 150
Б	КУП1	КУП (уравнивание потенциалов)		300	1120	

Ведомость отделки (на листе)

Марка	Поверхность	Материал, изделие	Цвет, код	Кол.
О3	потолок	окраска, Tikkurila, глубокоматовая	NCS S 0300-N	3 м²
О6	стены	облицовка плиткой, Italon Charme Extra, 600×1200 мм, 610015000370	Italon 610015000370 «Charme Extra»	7,5 м²

Ведомость изделий и проёмов (на листе)

Стена	Марка	Изделие, проём	На виде Ш×В, мм	Низ, мм
А	С-02	ванна	1500×600	0
Б	Д-4	дверь скрытого монтажа	700×2100	0
Б	С-03	умывальник	430×150	700

Примечания

1. Размеры — в мм от чистовых поверхностей стен; условные обозначения и общие указания — лист 12.
2. Облицовка — по сетке швов, раскладка от оси стены (треугольник у пола); подрезки — по листу раскладки плитки.
3. Гидроизоляция в 2 слоя, заход на стены 200 мм; над ванной — до 2000 и 300 мм за борт — до облицовки, с актом скрытых работ и тестом проливом (узел — на листе узлов).
4. Двери скрытого монтажа — полотно в плоскости стены, отделка стены по полотну, плинтус прерывается у короба (узел — на листе узлов).

	Лист	№ док.	Подпись	Дата
Дизайнер	Кырлан А.С.			14.11.26
Проверил				
Н. контр.				
Утв.				


Проект: Квартира 58 м² — **М 1:20**

Развёртки стен А, Б. Ванная (пом. 3)


Стадия	Лист	Листов
П	61	92

выпуск 14.11.2026 № 2b6bd7c078 · стр. 61 из 92

Стена В (М 1:20)

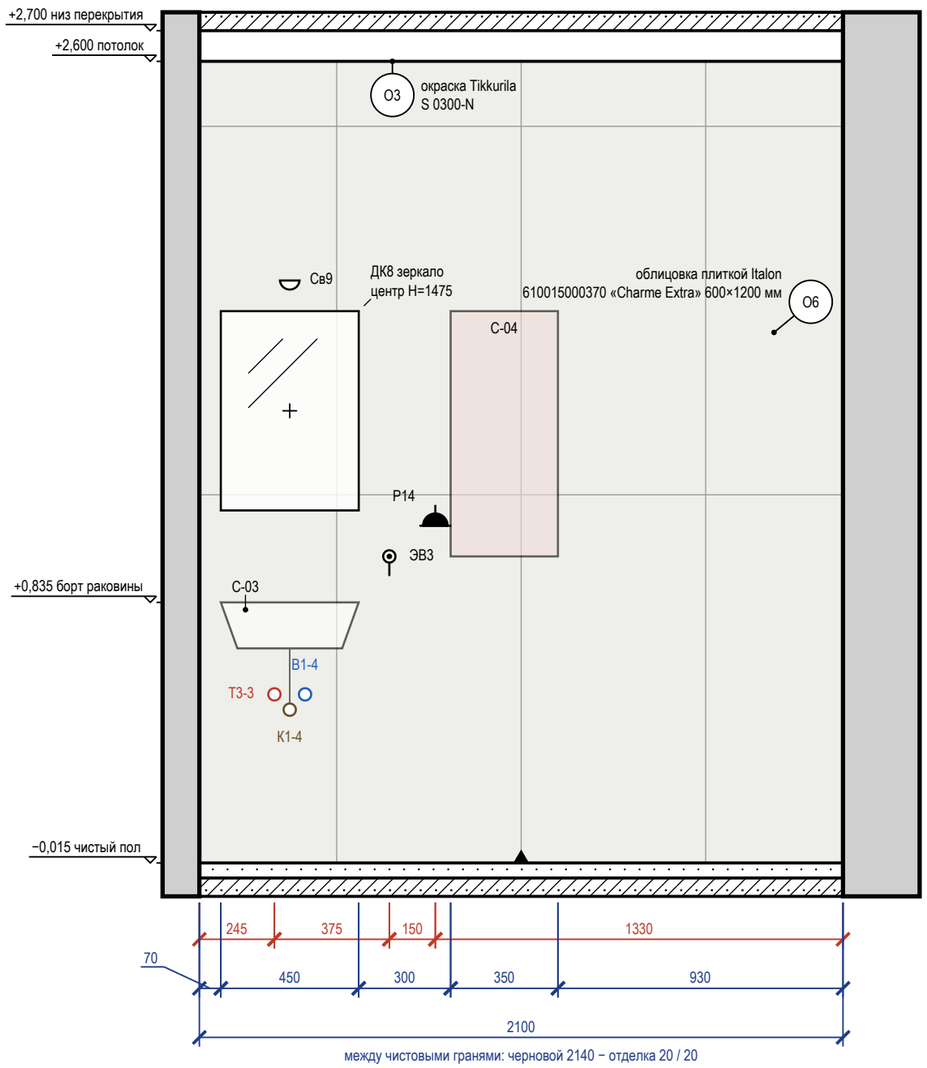


Стена Г (М 1:20)

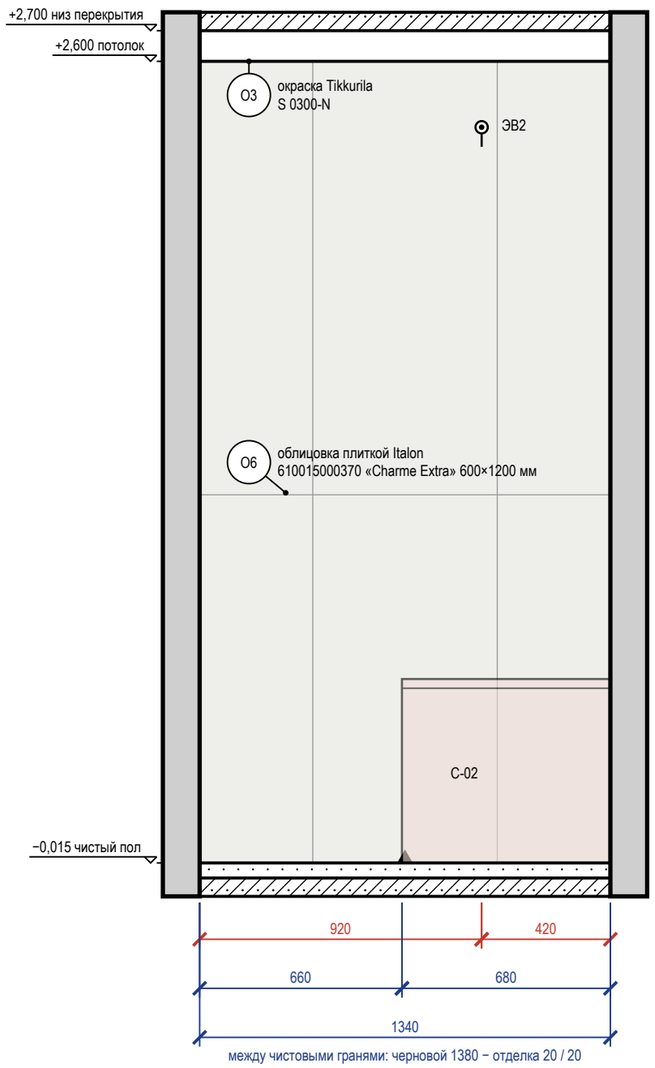

Стена В — визуализация, лист 8



Схема развёрток (М 1:50)

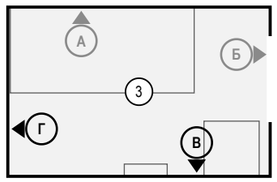

Ведомость точек и выводов

Стена	Марка	Что это	Гр.	H, мм	От угла, мм	Примечание
В	Т3-3	горячая вода — умывальник		550	245	межос. 100
В	К1-4	канализация — умывальник		500	295	Ø50
В	Св9	светильник настенный	1	1900	295	
В	В1-4	холодная вода — умывальник		550	345	межос. 100
В	ЭВ3	вывод кабеля: полотенцесушитель	5	1000	620	
В	Р14	розетка: фен	5	1100	770	IP44
Г	ЭВ2	вывод кабеля: вентилятор ВР2 (клавиша L4, таймер выбега)	1	2400	920	

Ведомость отделки (на листе)

Марка	Поверхность	Материал, изделие	Цвет, код	Кол.
О3	потолок	окраска, Tikkurila, глубокоматовая	NCS S 0300-N	3 м²
О6	стены	облицовка плиткой, Italon Charme Extra, 600×1200 мм, 610015000370	Italon 610015000370 «Charme Extra»	9 м²

Ведомость изделий и проёмов (на листе)

Стена	Марка	Изделие, проём	На виде Ш×В, мм	Низ, мм
В	С-03	умывальник	450×150	700
В	ДК8	зеркало	450×650	1150
В	С-04	полотенцесушитель	350×800	1000
Г	С-02	ванна	680×600	0

Примечания

1. Размеры — в мм от чистовых поверхностей стен; условные обозначения и общие указания — лист 12.
2. Облицовка — по сетке швов, раскладка от оси стены (треугольник у пола); подрезки — по листу раскладки плитки.
3. Гидроизоляция в 2 слоя, заход на стены 200 мм; над ванной — до 2000 и 300 мм за борт — до облицовки, с актом скрытых работ и тестом проливом (узел — на листе узлов).
4. Картины и зеркала крепить к основанию по паспорту изделия (закладные и анкеры — в перечне скрытых работ); крест — ось центра предмета.

	Лист	№ док.	Подпись	Дата
Дизайнер	Кырлан А.С.			14.11.26
Проверил				
Н. контр.				
Утв.				


Проект: Квартира 58 м² — **М 1:20**

Развёртки стен В, Г. Ванная (пом. 3)


Стадия	Лист	Листов
П	62	92

выпуск 14.11.2026 № 2b6bd7c078 · стр. 62 из 92

Стена А (М 1:20)

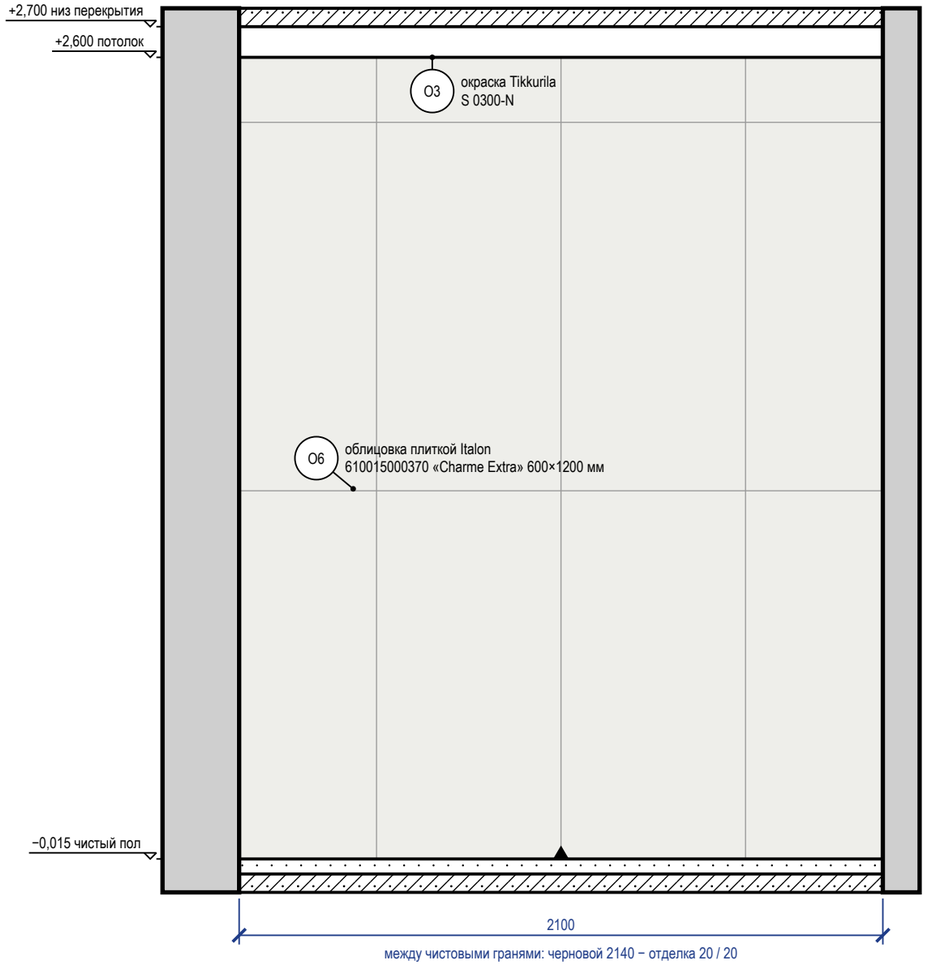


Стена Б (М 1:20)

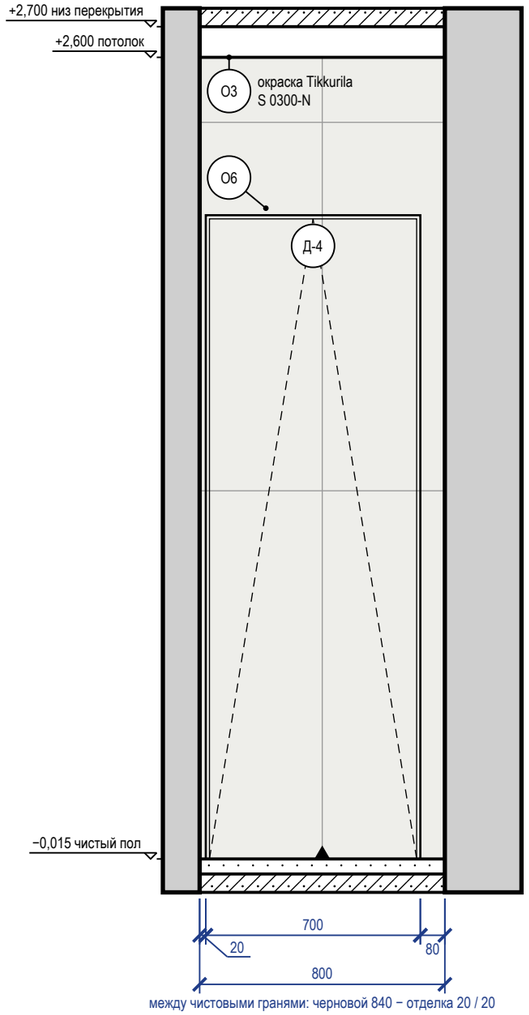

1 Порог 15 мм: мокрая зона — смежное помещение (М 1:5)


Узел 1 — лист С12

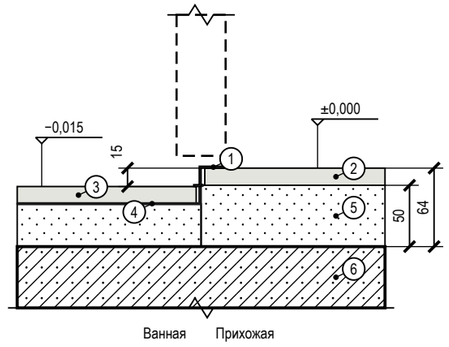

Поз.	Состав слоя, изделие
1	порог-переход металлический, перепад 15 мм, на клей-герметик
2	керамогранит на клею С2 TE S1
3	керамогранит на клею С2 TE S1
4	гидроизоляция в 2 слоя с подъёмом на торец ступени, лента в углу
5	ЦПС М200 50 мм; в мокрой зоне 33 мм
6	плита перекрытия

2 Дверь скрытого монтажа в плоскости стены, плинтус (М 1:10)

Узел 2 — лист С12

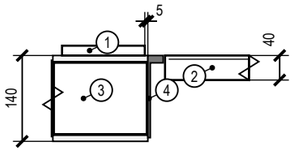


Поз.	Состав слоя, изделие
1	плинтус МДФ 110×16 на клей; у короба зазор 5 мм, окраска в цвет стены
2	полотно 40 мм под окраску, заподлицо со стеной; теневой шов 3 мм
3	стена 120 мм, штукатурка 10 мм с двух сторон
4	короб скрытого монтажа (алюминий), лицом в плоскости отделки; монтаж до штукатурки

Ведомость отделки (на листе)

Марка	Поверхность	Материал, изделие	Цвет, код	Кол.
О3	потолок	окраска, Tikkurila, глубокоматовая	NCS S 0300-N	1,8 м²
О6	стены	облицовка плиткой, Italon Charme Extra, 600×1200 мм, 610015000370	Italon 610015000370 «Charme Extra»	6,1 м²

Схема развёрток (М 1:50)

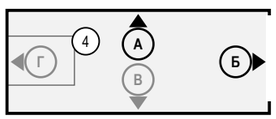

Ведомость изделий и проёмов (на листе)

Стена	Марка	Изделие, проём	На виде Ш×В, мм	Низ, мм
Б	Д-4	дверь скрытого монтажа	700×2100	0

Примечания

1. Размеры — в мм от чистовых поверхностей стен; условные обозначения и общие указания — лист 12.
2. Облицовка — по сетке швов, раскладка от оси стены (треугольник у пола); подрезки — по листу раскладки плитки.
3. Гидроизоляция в 2 слоя, заход на стены 200 мм — до облицовки, с актом скрытых работ и тестом проливом (узел — на листе узлов).
4. Двери скрытого монтажа — полотно в плоскости стены, отделка стены по полотну, плинтус прерывается у короба (узел — на листе узлов).

	Лист	№ док.	Подпись	Дата
Дизайнер	Кырлан А.С.			14.11.26
Проверил				
Н. контр.				
Утв.				


Проект: Квартира 58 м² — **М 1:20**

Развёртки стен А, Б. Санузел (пом. 4)


Стадия	Лист	Листов
П	63	92

выпуск 14.11.2026 № 2b6bd7c078 · стр. 63 из 92

Стена В (М 1:20)

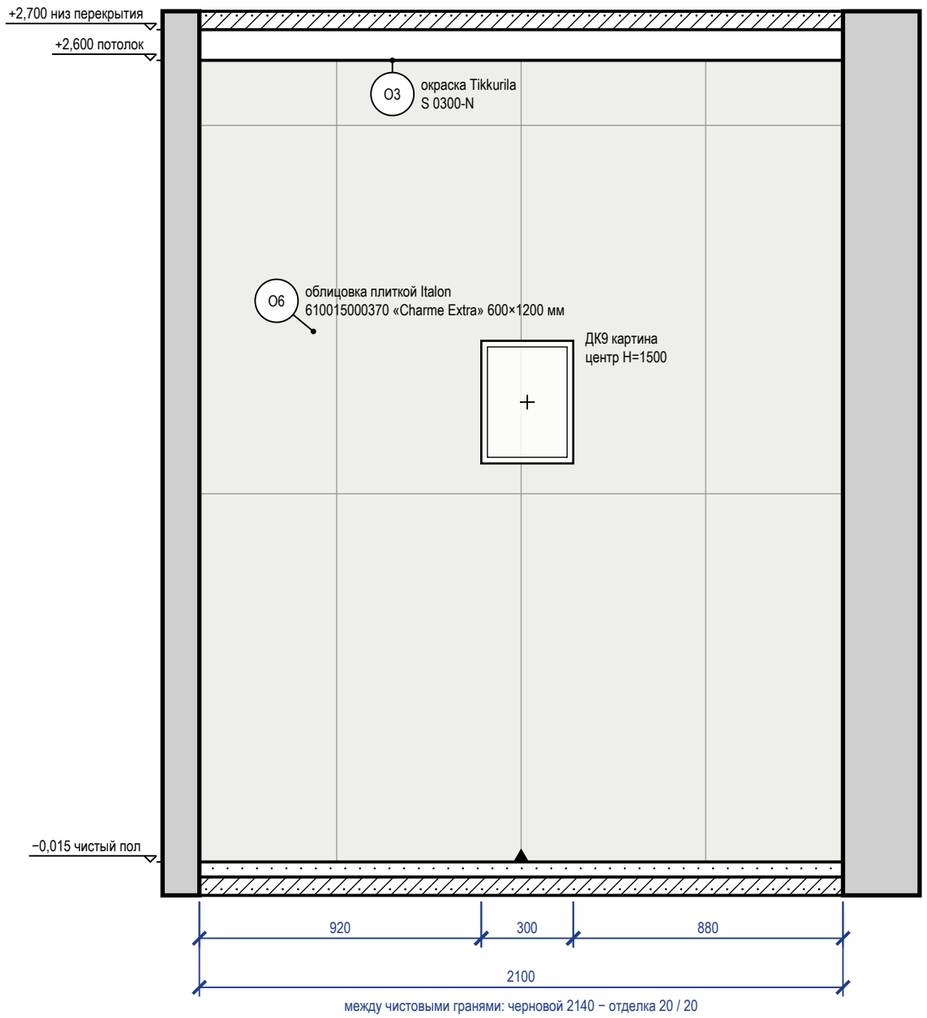

Стена Г (М 1:20)

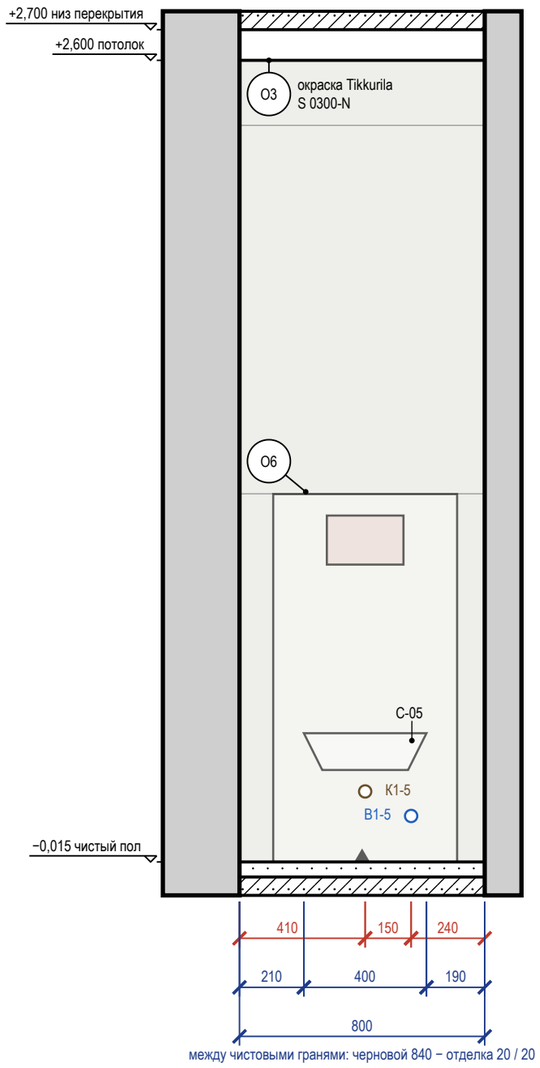

Ведомость точек и выводов

Стена	Марка	Что это	Гр.	H, мм	От угла, мм	Примечание
Г	К1-5	канализация — унитаз подвесной		230	410	Ø110
Г	В1-5	холодная вода — унитаз подвесной		150	560	в раме инсталляции


Стена В — визуализация, лист 9



Ведомость отделки (на листе)

Марка	Поверхность	Материал, изделие	Цвет, код	Кол.
О3	потолок	окраска, Tikkurila, глубокоматовая	NCS S 0300-N	1,8 м²
О6	стены	облицовка плиткой, Italon Charme Extra, 600×1200 мм, 610015000370	Italon 610015000370 «Charme Extra»	7,6 м²

Схема развёрток (М 1:50)

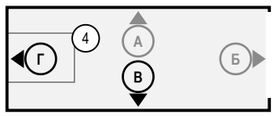

Ведомость изделий и проёмов (на листе)

Стена	Марка	Изделие, проём	На виде Ш×В, мм	Низ, мм
В	ДК9	картина	300×400	1300
Г	С-05	унитаз подвесной	400×120	300

Примечания

1. Размеры — в мм от чистовых поверхностей стен; условные обозначения и общие указания — лист 12.
2. Схема мебели, приборов и декора не является технической документацией для производства мебели; габариты — по паспортам изделий.
3. Облицовка — по сетке швов, раскладка от оси стены (треугольник у пола); подрезки — по листу раскладки плитки.
4. Гидроизоляция в 2 слоя, заход на стены 200 мм — до облицовки, с актом скрытых работ и тестом проливом (узел — на листе узлов).
5. Картины и зеркала крепить к основанию по паспорту изделия (закладные и анкеры — в перечне скрытых работ); крест — ось центра предмета.

	Лист	№ док.	Подпись	Дата	Проект: Квартира 58 м²	М 1:20
Дизайнер	Кырлан А.С.			14.11.26	Развёртки стен В, Г. Санузел (пом. 4)	Стадия: П; Лист: 64; Листов: 92
Проверил						
Н. контр.						
Утв.						

выпуск 14.11.2026 № 2b6bd7c078 · стр. 64 из 92

Стена А (М 1:20)


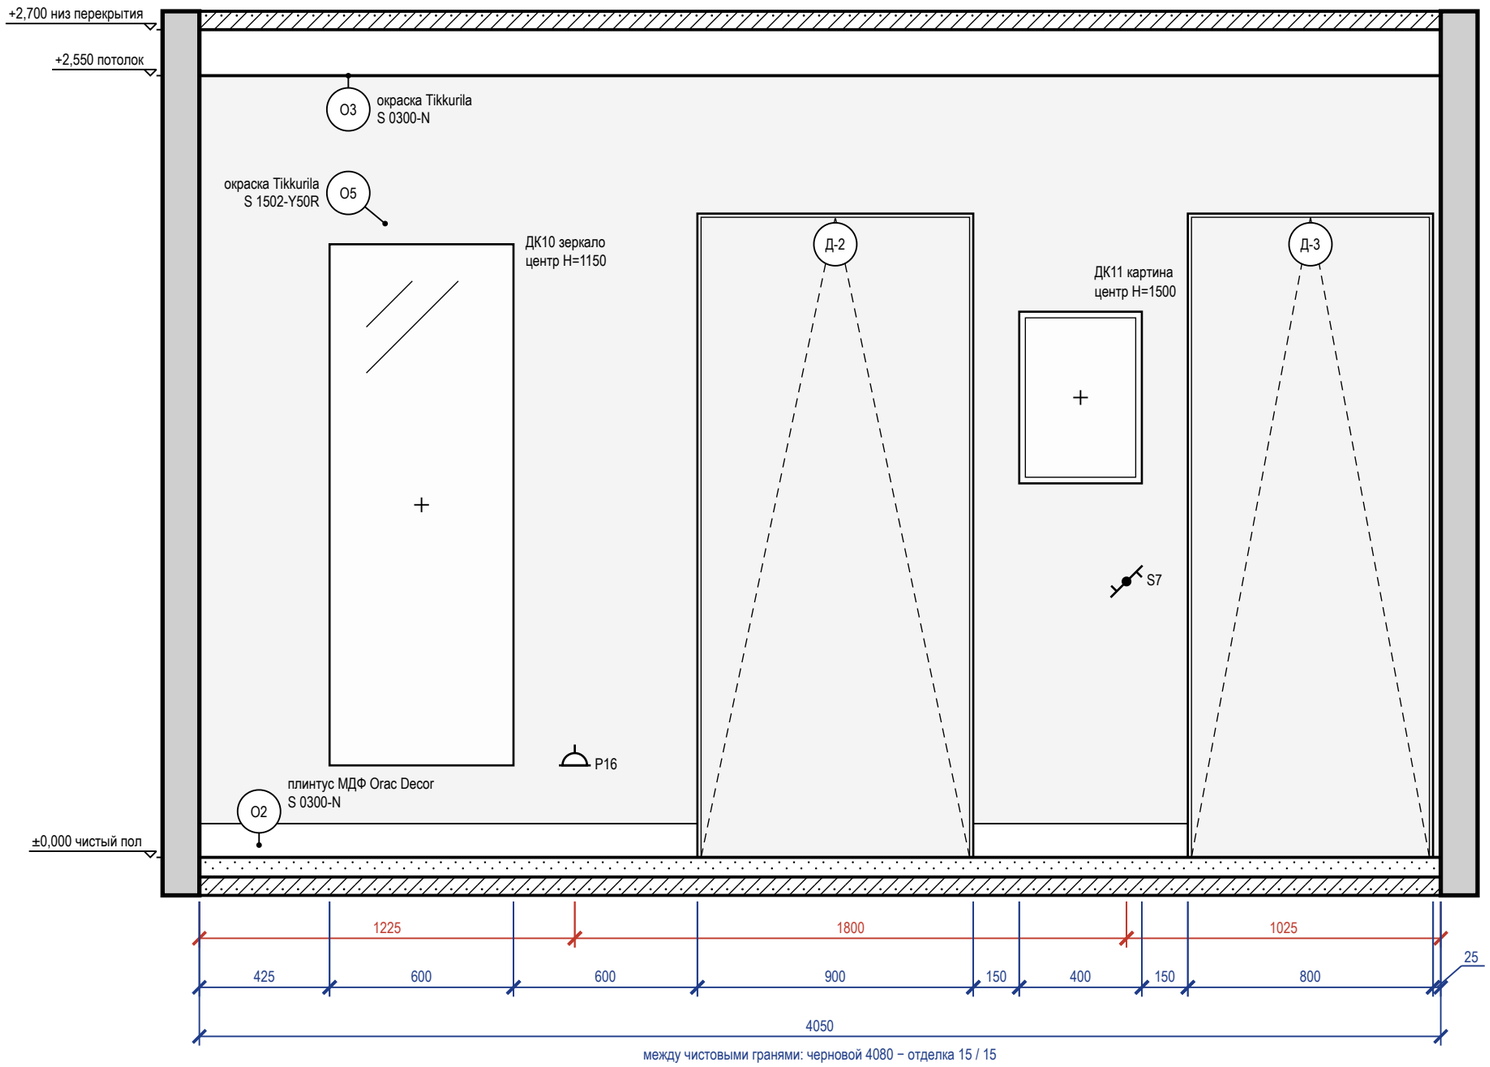


Схема развёрток (М 1:50)

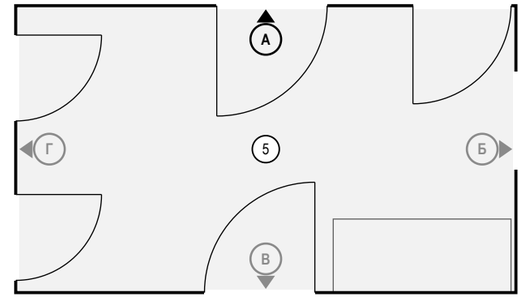

Ведомость точек и выводов

Марка	Что это	Гр.	Н, мм	От угла, мм	Примечание
Р16	розетка: уборка	4	300	1225	
S7	выключатель	1	900	3025	

Ведомость отделки (на листе)

Марка	Поверх ность	Материал, изделие	Цвет, код	Кол.
О2	плинтус	плинтус МДФ, Orac Decor Luxxus, h 110 мм, SX184, шелковисто-матовая	NCS S 0300-N	2,3 м
О3	потолок	окраска, Tikkurila, глубокоматовая	NCS S 0300-N	9,6 м²
О5	стены	окраска, Tikkurila, шелковисто-матовая, подготовка Q3	NCS S 1502-Y50R	6,8 м²

Ведомость изделий и проёмов (на листе)

Марка	Изделие, проём	На виде Ш×В, мм	Низ, мм
ДК10	зеркало	600×1700	300
Д-2	дверь скрытого монтажа	900×2100	0
ДК11	картина	400×560	1220
Д-3	дверь скрытого монтажа	800×2100	0

Примечания

1. Размеры — в мм от чистовых поверхностей стен; условные обозначения и общие указания — лист 12.
2. Картины и зеркала крепить к основанию по паспорту изделия (закладные и анкеры — в перечне скрытых работ); крест — ось центра предмета.
3. Двери скрытого монтажа — полотно в плоскости стены, отделка стены по полотну, плинтус прерывается у короба (узел — на листе узлов).
4. Потолок — у каждой стены свой, по плану потолков (ПТ1); ступени — зоной, кромка короба перед нишей — тонкой линией; в поле потолка: ПТ2 +2,600.

	Лист	№ док.	Подпись	Дата
Дизайнер	Кырлан А.С.			14.11.26
Проверил				
Н. контр.				
Утв.				


Проект: Квартира 58 м² — **М 1:20**

Развёртка стены А. Прихожая (пом. 5)


Стадия	Лист	Листов
П	65	92

выпуск 14.11.2026 № 2b6bd7c078 · стр. 65 из 92

Стена Б (М 1:20)

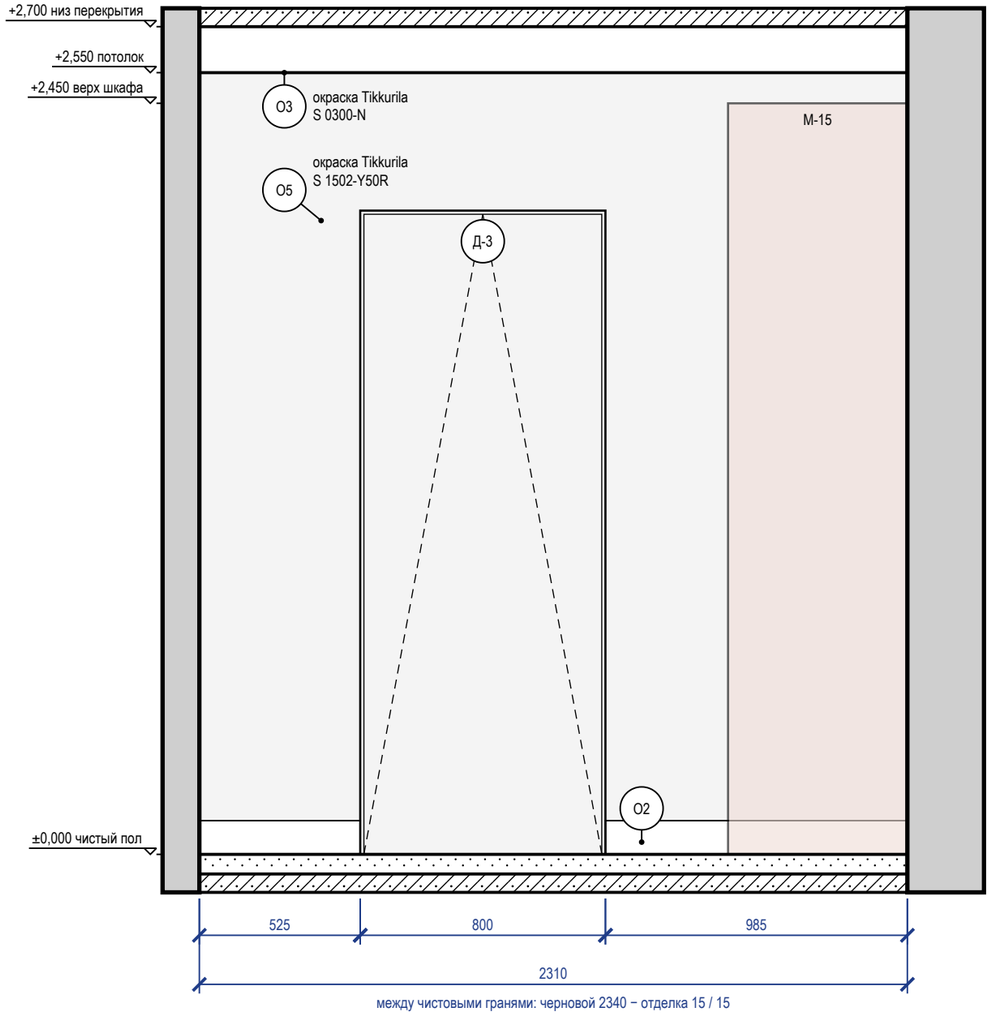


Стена Б — визуализация, лист 10

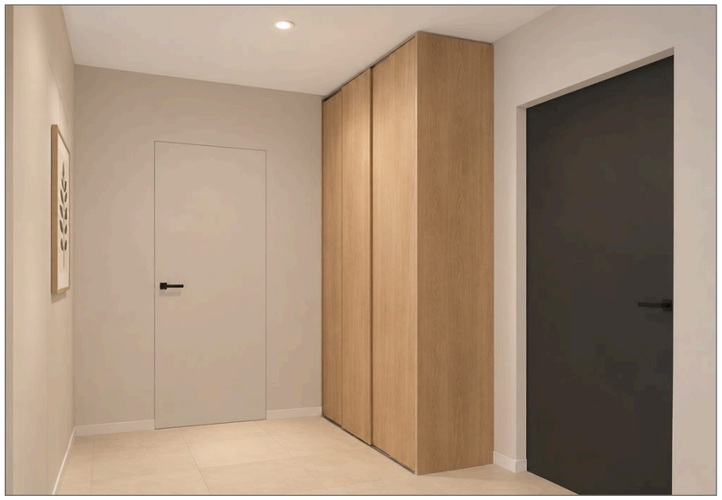

Ведомость отделки (на листе)

Марка	Поверхность	Материал, изделие	Цвет, код	Кол.
О2	плинтус	плинтус МДФ, Orac Decor Luxxus, h 110 мм, SX184, шелковисто-матовая	NCS S 0300-N	1,5 м
О3	потолок	окраска, Tikkurila, глубокоматовая	NCS S 0300-N	9,6 м²
О5	стены	окраска, Tikkurila, шелковисто-матовая, подготовка Q3	NCS S 1502-Y50R	4,2 м²

Схема развёрток (М 1:50)

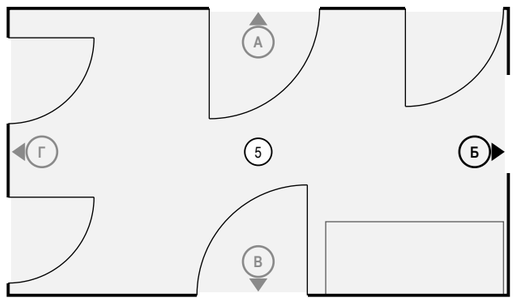

Ведомость изделий и проёмов (на листе)

Марка	Изделие, проём	На виде Ш×В, мм	Низ, мм
Д-3	дверь скрытого монтажа	800×2100	0
М-15	шкаф-купе	585×2450	0

Примечания

1. Размеры — в мм от чистовых поверхностей стен; условные обозначения и общие указания — лист 12.
2. Двери скрытого монтажа — полотно в плоскости стены, отделка стены по полотну, плинтус прерывается у короба (узел — на листе узлов).
3. Потолок — у каждой стены свой, по плану потолков (ПТ1); ступени — зоной, кромка короба перед нишей — тонкой линией; в поле потолка: ПТ2 +2,600.

	Лист	№ док.	Подпись	Дата	Проект: Квартира 58 м²	М 1:20
Дизайнер	Кырлан А.С.			14.11.26	Развёртка стены Б. Прихожая (пом. 5)	
Проверил						
Н. контр.						
Утв.						

Стадия	Лист	Листов
П	66	92

выпуск 14.11.2026 № 2b6bd7c078 · стр. 66 из 92

Стена В (М 1:20)


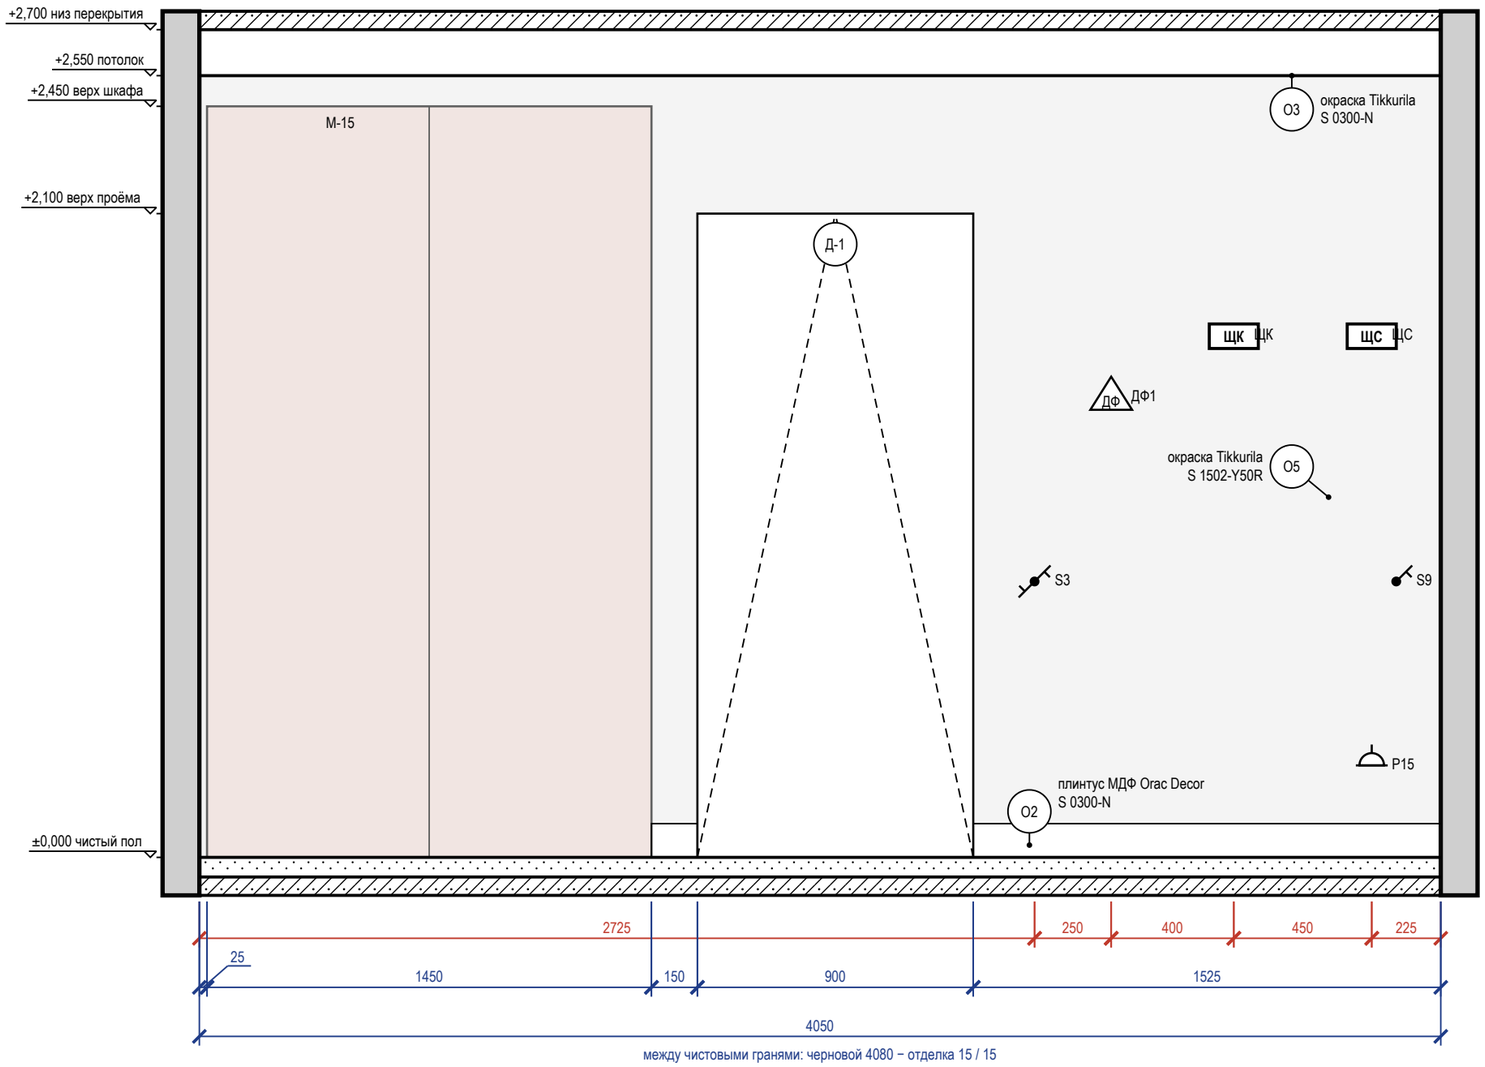


Схема развёрток (М 1:50)

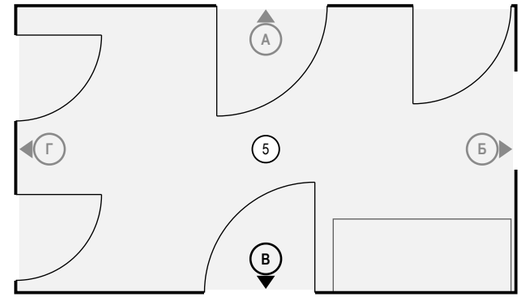

Ведомость точек и выводов

Марка	Что это	Гр.	Н, мм	От угла, мм	Примечание
S3	выключатель	1	900	2725	
ДФ1	домофон: трубка домофона		1500	2975	
ЩК	щит		1700	3375	
P15	розетка: питание ЩС (роутер, ИБП)	4	300	3825	
ЩС	щит: щит слаботочный: ввод провайдера, роутер		1700	3825	
S9	выключатель: свет санузла (пом. 4)	1	900	3905	

Ведомость отделки (на листе)

Марка	Поверхность	Материал, изделие	Цвет, код	Кол.
О2	плинтус	плинтус МДФ, Orac Decor Luxxus, h 110 мм, SX184, шелковисто-матовая	NCS S 0300-N	1,7 м
О3	потолок	окраска, Tikkurila, глубокоматовая	NCS S 0300-N	9,6 м²
О5	стены	окраска, Tikkurila, шелковисто-матовая, подготовка Q3	NCS S 1502-Y50R	8,4 м²

Ведомость изделий и проёмов (на листе)

Марка	Изделие, проём	На виде Ш×В, мм	Низ, мм
М-15	шкаф-купе	1450×2450	0
Д-1	дверь	900×2100	0

Примечания

1. Размеры — в мм от чистовых поверхностей стен; условные обозначения и общие указания — лист 12.
2. Потолок — у каждой стены свой, по плану потолков (ПТ1); ступени — зоной, кромка короба перед нишей — тонкой линией; в поле потолка: ПТ2 +2,600.

	Лист	№ док.	Подпись	Дата
Дизайнер	Кырлан А.С.			14.11.26
Проверил				
Н. контр.				
Утв.				

Проект: Квартира 58 м² — **М 1:20**

Развёртка стены В. Прихожая (пом. 5)

Стадия	Лист	Листов
П	67	92

выпуск 14.11.2026 № 2b6bd7c078 · стр. 67 из 92

Стена Г (М 1:20)


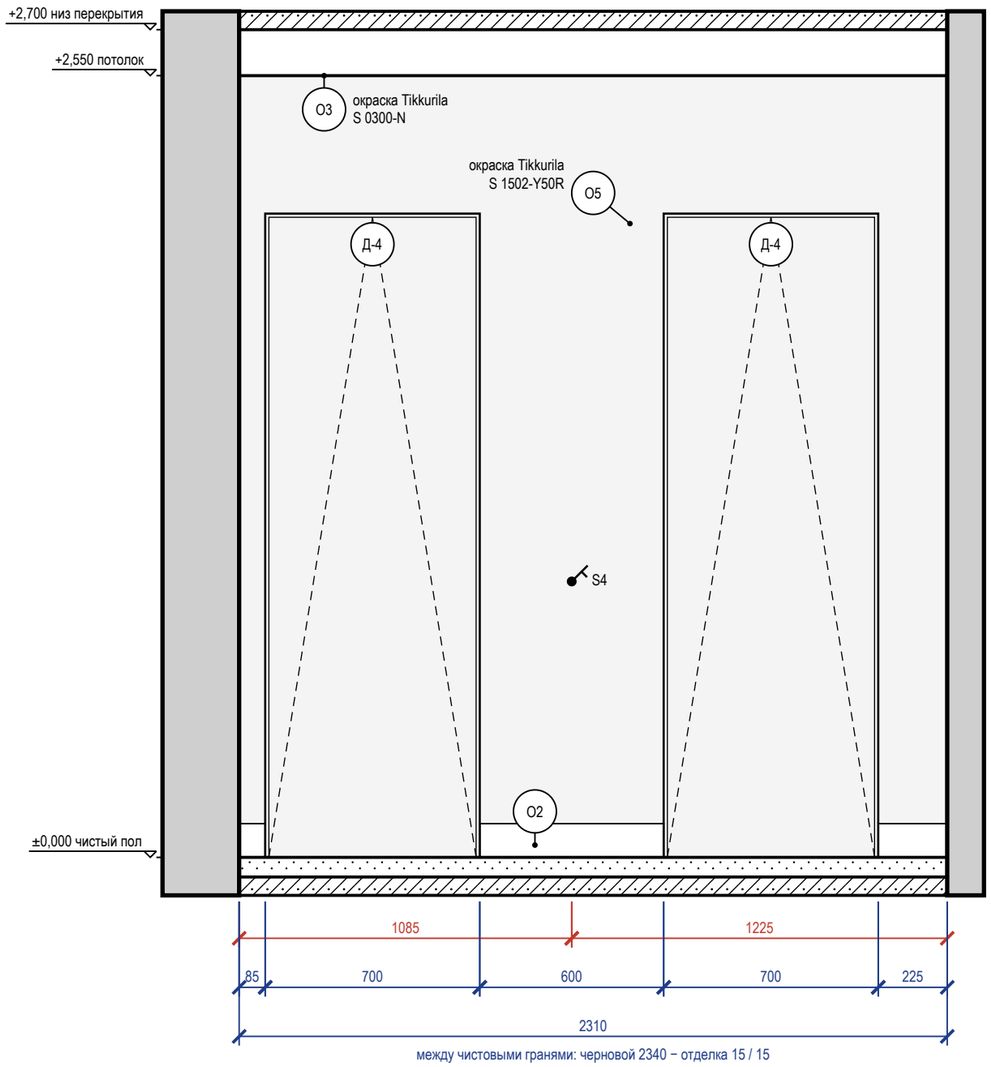


Схема развёрток (М 1:50)

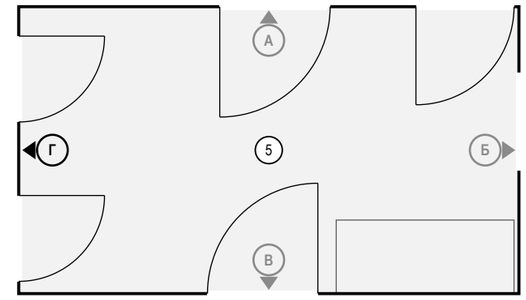

Ведомость точек и выводов

Марка	Что это	Гр.	Н, мм	От угла, мм	Примечание
S4	выключатель: свет ванной (пом. 3)	1	900	1085	

Ведомость отделки (на листе)

Марка	Поверхность	Материал, изделие	Цвет, код	Кол.
О2	плинтус	плинтус МДФ, Orac Decor Luxxus, h 110 мм, SX184, шелковисто-матовая	NCS S 0300-N	0,9 м
О3	потолок	окраска, Tikkurila, глубокоматовая	NCS S 0300-N	9,6 м²
О5	стены	окраска, Tikkurila, шелковисто-матовая, подготовка Q3	NCS S 1502-Y50R	3 м²

Ведомость изделий и проёмов (на листе)

Марка	Изделие, проём	На виде Ш×В, мм	Низ, мм
Д-4	дверь скрытого монтажа	700×2100	0


Примечания

1. Размеры — в мм от чистовых поверхностей стен; условные обозначения и общие указания — лист 12.
2. Двери скрытого монтажа — полотно в плоскости стены, отделка стены по полотну, плинтус прерывается у короба (узел — на листе узлов).
3. Потолок — у каждой стены свой, по плану потолков (ПТ1); ступени — зоной, кромка короба перед нишей — тонкой линией; в поле потолка: ПТ2 +2,600.


	Лист	№ док.	Подпись	Дата	Проект: Квартира 58 м²	М 1:20
Дизайнер	Кырлан А.С.			14.11.26	Развёртка стены Г. Прихожая (пом. 5)	Стадия: П; Лист: 68; Листов: 92
Проверил						
Н. контр.						
Утв.						

выпуск 14.11.2026 № 2b6bd7c078 · стр. 68 из 92

Стена А (М 1:20)

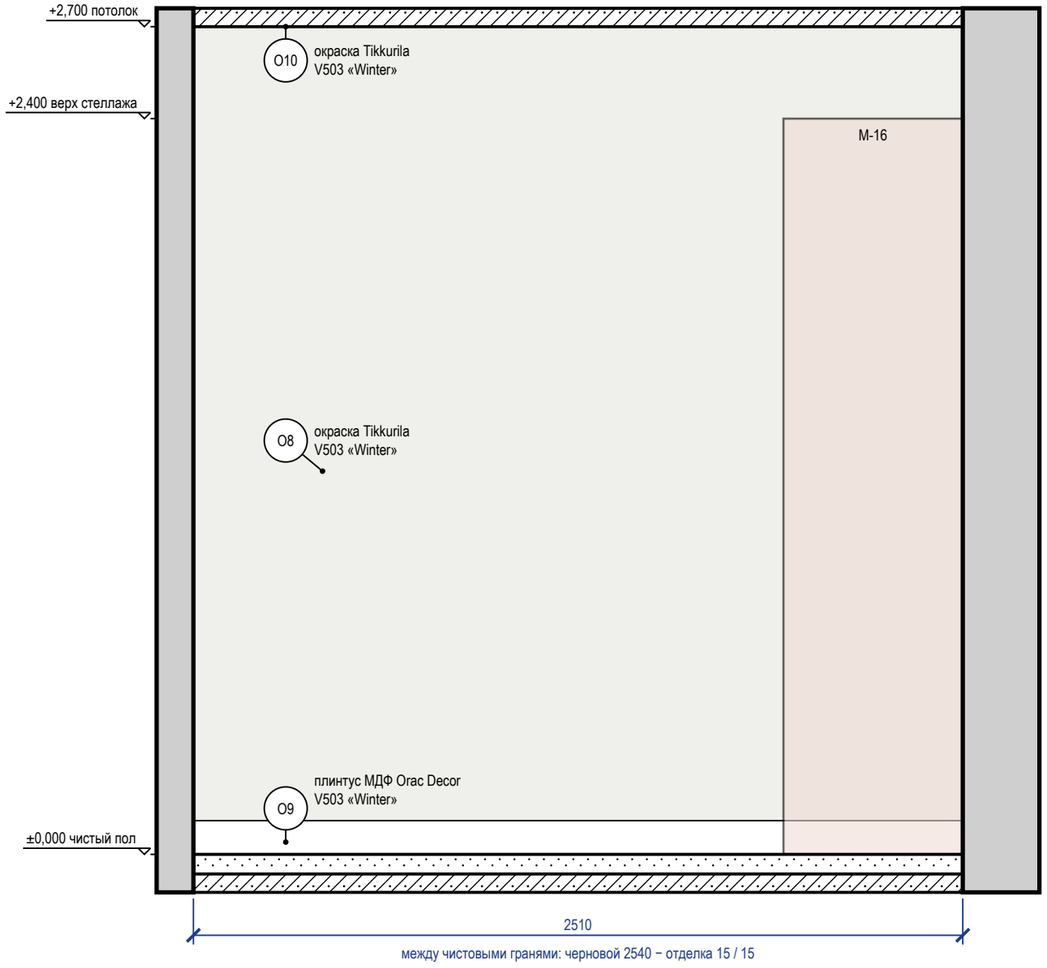

Стена Б (М 1:20)

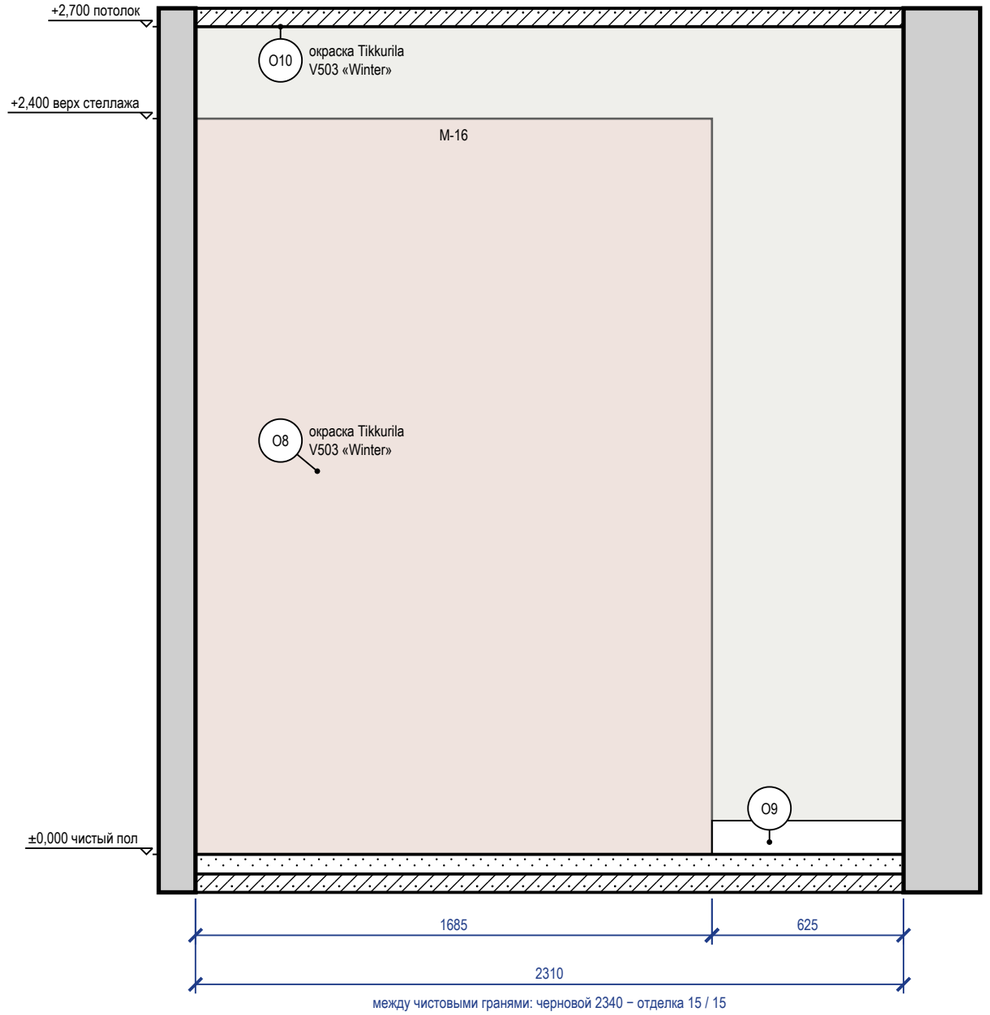


Стена Б — визуализация, лист 11



Ведомость отделки (на листе)

Марка	Поверхность	Материал, изделие	Цвет, код	Кол.
O8	стены	окраска, Tikkurila Harmony, матовая, подготовка Q3	Tikkurila V503 «Winter»	13 м²
O9	плинтус	плинтус МДФ, Orac Decor Luxxus, h 110 мм, SX184	Tikkurila V503 «Winter»	3,1 м
O10	потолок	окраска, Tikkurila Anti-Reflex 2, глубокоматовая, подготовка Q3	Tikkurila V503 «Winter»	5,9 м²

Схема развёрток (М 1:50)

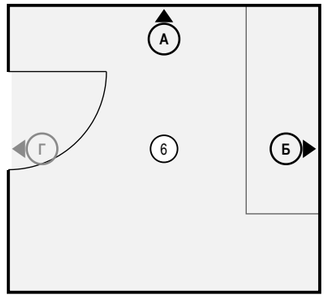

Примечания

1. Размеры — в мм от чистовых поверхностей стен; условные обозначения и общие указания — лист 12.

	Лист	№ док.	Подпись	Дата	Проект: Квартира 58 м²			М 1:20
Дизайнер	Кырлан А.С.			14.11.26	Развёртки стен А, Б. Гардеробная (пом. 6)	Стадия	Лист	Листов
Проверил						П	69	92
Н. контр.								
Утв.								

выпуск 14.11.2026 № 2b6bd7c078 · стр. 69 из 92

Стена Г (М 1:20)


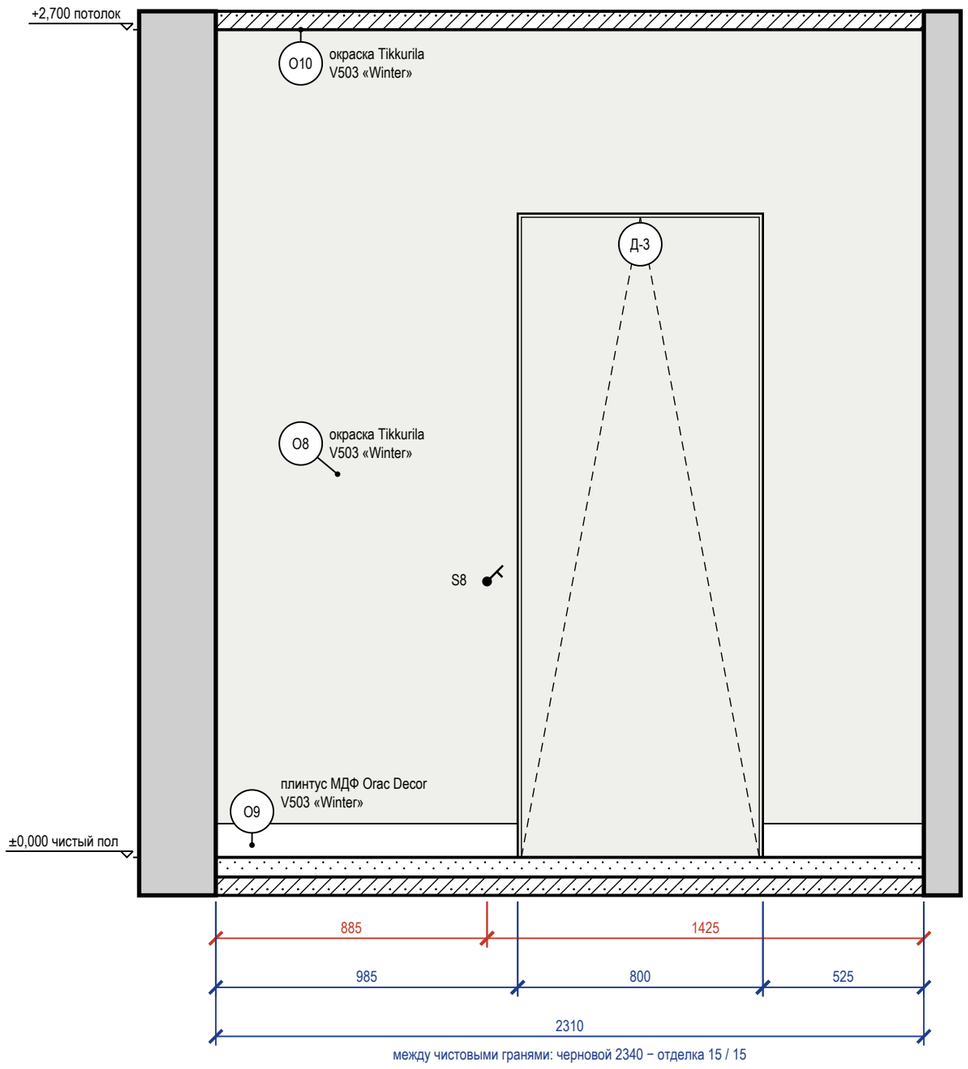


Схема развёрток (М 1:50)

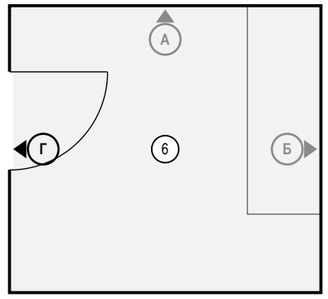

Ведомость точек и выводов

Марка	Что это	Гр.	Н, мм	От угла, мм	Примечание
S8	выключатель: свет гардеробной	1	900	885	

Ведомость отделки (на листе)

Марка	Поверх ность	Материал, изделие	Цвет, код	Кол.
О8	стены	окраска, Tikkurila Harmony, матовая, подготовка Q3	Tikkurila V503 «Winter»	4,6 м²
О9	плинтус	плинтус МДФ, Orac Decor Luxxus, h 110 мм, SX184	Tikkurila V503 «Winter»	1,5 м
О10	потолок	окраска, Tikkurila Anti-Reflex 2, глубокоматовая, подготовка Q3	Tikkurila V503 «Winter»	5,9 м²

Ведомость изделий и проёмов (на листе)

Марка	Изделие, проём	На виде Ш×В, мм	Низ, мм
Д-3	дверь скрытого монтажа	800×2100	0

Примечания

1. Размеры — в мм от чистовых поверхностей стен; условные обозначения и общие указания — лист 12.
2. Двери скрытого монтажа — полотно в плоскости стены, отделка стены по полотну, плинтус прерывается у короба (узел — на листе узлов).

	Лист	№ док.	Подпись	Дата	Проект: Квартира 58 м²			М 1:20
Дизайнер	Кырлан А.С.			14.11.26	Развёртка стены Г. Гардеробная (пом. 6)	Стадия	Лист	Листов
Проверил						П	70	92
Н. контр.								
Утв.								

выпуск 14.11.2026 № 2b6bd7c078 · стр. 70 из 92

Комплект предварительный по пунктам этих таблиц. Пока по пункту нет ответа или решения, показанное на указанном листе — допущение проектировщика, а не утверждённое решение.
Сводка: открытых вопросов — 7 (из них ждут факта объекта — 6: контрольного обмера, обследования или документа); изменений в реестре — 5, из них без подписи — 2.

Открытые вопросы и принятые допущения

№	Формулировка	Вид	Кто решает	Если решения нет	Лист, где это проявляется
К-1	Вентканалы на плане заказчика не показаны: ВК-1 принят у перегородки ванной и санузла (со стороны прихожей), ВК-2 — у кухни. От них зависят решётки ВР1–ВР3 и короба. Замерить положение и сечение каналов, проверить тягу.	Отсутствует Ждёт: обмера	Инженер ОВ	решётки ванной и санузла — у ВК-1, кухни — у ВК-2; места — до обмера, лист перевыпустить по факту	л. 49 — План вентиляции
К-2	Ванная (пом. 3), 2140 × 1380 мм в чистоте, проём Д-4 у стены Б. Расстановка проектировщика: ванна 1500 × 700 у стены А от стены Г (была 1600 и заходила в проход перед Д-4 — свободно 240 из 700 мм), умывальник С-03 у стены В справа от ванны — перед ним свободно 750 мм (был напротив ванны в 230 мм), полотенцесушитель С-04 на стене В между коробом стояков и умывальником. Унитаз П2 из образца раскладки снят: он стоял на стояке Ст К1-1 (короба и люка не поставить), унитаз квартиры — С-05 в санузле, инсталляция и короб — там. Остаётся: перед ванной 680 мм до стены В при ориентире 750 мм — это глубина помещения; у умывальника до стены Б 90 мм при ориентире 200 мм. Решить: (а) принять расстановку; (б) душ с поддоном 900 × 900 у стены Г вместо ванны — перед приборами ≥ 750 мм, кадры ванной перерисовать; (в) другой вариант автора.	Спорно Ждёт: решения	Инженер ВК (вода, канализация)	ванна 1500 × 700 и умывальник у стены В по листам; модели ванны и умывальника не заказывать до решения	л. 25 — План выводов сантехники л. 20 — План размещения мебели и оборудования
К-3	Скрытые двери Д-2, Д-3, Д-4 стоят в существующих проёмах прихожей, размеров в свету нет: короб скрытой двери шире и выше полотна на 100–120 / 50–80 мм, полотно по проёму 2100 под ряд 2000 не встаёт (по каталогам нужно 2050–2080). У Д-3 (спальня) и Д-4 (санузел) откос от угла 40 мм — под короб нужно не меньше 50. Замерить проёмы в чистоте и откосы; решить: проёмы подрезать/расширить на 10+ мм от угла (если стена не несущая) или взять модель с узким коробом; высоту проёма — по выбранной модели.	Отсутствует Ждёт: обмера, затем решения	Архитектор-планировщик	блоки скрытых дверей не заказывать до замера; полотна на листах — расчётные («расч.»), проёмы не переносятся	л. 36 — План размещения дверей
К-4	Климатический подрайон (СП 131.13330) не задан: принят не северный — жилые комнаты и кухня под потолком от 2,5 м (СП 54, п. 5.12); в IA, IБ, IГ, IД, IVA — от 2,7 м.	Отсутствует Ждёт: документа	Архитектор-планировщик	отметки потолков жилых — по 2,5 м; при северном подрайоне уровни ниже 2,7 м пересчитать до заказа каркаса	л. 38 — План потолков
К-5	Основа альбома — план заказчика без контрольного обмера: размеры помещений сняты с плана, высота потолка 2700 мм и толщины стен (наружные 250 мм, перегородки 120 мм) приняты — на плане они не указаны. От них зависят вертикальные размеры (развёртки, шкафы, плитка, потолки), объёмы работ и сборка шкафов-купе. Выполнить контрольный обмер.	Непонятно Ждёт: обмера	Архитектор-планировщик	размеры, высота потолка и толщины стен — принятые; мебель на заказ, двери и каркас потолков не заказывать до обмера	л. 14 — План планировки от заказчика
К-6	Разрешённая мощность 15 кВт принята по типовой квартире, технических условий в материалах объекта нет. Сверить с техническими условиями.	Непонятно Ждёт: документа	Инженер-электрик	вводной аппарат и группы щита — по 15 кВт; при меньшей мощности схему щита пересчитать до монтажа	л. 41 — Однолинейная схема щита
К-7	Места стиральной машины в квартире не было. В ванной 2,2 × 1,5 м и санузле места 600 × 600 с подходом нет. Предложение исполнителя: узкая машина 600 × 450 под столешницей кухни вместо модуля с ящиками М-05 справа от варочной, ряд удлиняется на 220 мм; отдельная группа щита с УЗО 30 мА. Решить: принять, или машина в ванной вместо ванны (душ), или отказ от машины (прачечная) решением автора	Предложение Ждёт: документа, затем решения	Инженер ВК (вода, канализация)	стиральная машина ОБ-02 в кухне под столешницей (ниша вместо М-05, 2800…3420) — как на листах	л. 25 — План выводов сантехники л. 20 — План размещения мебели и оборудования л. 41 — Однолинейная схема щита

	Лист	№ док.	Подпись	Дата
Дизайнер	Кырлан А.С.			14.11.26
Проверил				
Н. контр.				
Утв.				

Проект: Квартира 58 м²

Открытые вопросы, принятые допущения и конфликты. Лист 1 из 2

Стадия	Лист	Листов
П	71	92

выпуск 14.11.2026 № 2b6bd7c078 · стр. 71 из 92

Изменения проекта после выпуска листов (реестр изменений)


№	Дата	Лист	Было	Стало	Кто решил, подпись
ИЗ-1	30.10.2026	л. 44 — План розеток и электровыводов л. 48 — Управление светильниками л. 46 — План освещения л. 24 — Ведомости изделий, техники и фурнитуры	Кухня-гостиная: ТВ1, LAN1 и розетка «ТВ, приставка» стояли на стене В (привязка 3300…3450, кухонная стена), а ТВ-тумба ОБ-01 — на стене Г (1500…3300): за телевизором точек не было. Выключатель S1 — на стене Г в зоне экрана, у двери Д-2 выключателя не было. Светильник гардеробной Св16 — на линии L6 подсветки кухонной столешницы, выключателя в гардеробной нет. Ванная и санузел — одна линия L4 с одним выключателем S4. Вытяжка в М-07 без вывода питания; розетка холодильника без привязки к модулю М-01.	ТВ1 (2400), LAN1 (2550) и розетка приставки (2400, H=300) — на стене Г по оси тумбы ОБ-01. S1 стена В, привязка 4950 (150 мм от проёма Д-2 со стороны ручки), S5 у дивана — проходной. Св16 — линия L7, выключатель S8 на стене Г гардеробной у Д-3 (привязка 1500). Санузел — линия L9, выключатель S9 в прихожей у Д-4 санузла (стена Г, привязка 1450); S4 — только ванная (L4, вентилятор ВР2). Розетка вытяжки — стена В привязка 2500, H=2200, группа 2 (для М-07); розетка холодильника — для М-01.	Утверждено: Кырлан А.С., 12.11.2026. Предложил: исполнитель.
ИЗ-2	30.10.2026	л. 20 — План размещения мебели и оборудования л. 21 — Спецификация мебели и оборудования	Диван М-08 на стене Б привязка 1300…3500: торец в 500 мм от стены В, дверь Д-2 (3900…4800) открывалась в торец дивана. Кресло М-11 х 4250, у 450.	Диван М-08 привязка 1000…3200 — перед проёмом 800 мм; кресло М-11 х 3500…4300, у 450 у окна 2. Выключатель S5 и розетка у дивана — привязка 900. Знак «**» у М-08, М-11 до подписи автора.	Утверждено: Кырлан А.С., 12.11.2026. Предложил: исполнитель.
ИЗ-3	30.10.2026	л. 49 — План вентиляции	Внутренний блок КВ-1 на стене А привязка 3300…4200 — внутри оконного проёма 3200…4800; наружный КН-1 привязка 3350 — на окне.	КВ-1 — стена Г, привязка 300…1200 (простенок у окна 1), КН-1 — стена А, простенок между окнами 2400…3200. Трасса ≈ 3 м (петля принята по минимуму, паспорта модели нет). Знак «**» у КВ-1 до подписи автора.	Утверждено: Кырлан А.С., 12.11.2026. Предложил: исполнитель.
ИЗ-4	12.11.2026	полный альбом	Декор и текстиль в данных проекта не были заданы: ни штор, ни ковров, ни подушек и пледов, ни картин, зеркал и растений (в палитре — пометка «текстиль в данных ещё не задан»). Кадры визуализаций и листы декоратора строятся только по данным — помещения выходили пустыми; зеркал в прихожей и над умывальником ванной не было.	Декор и текстиль заданы позициями плана. Кухня-гостиная: шторы льняные в пол на оба окна (Т1, Т2; шина на потолке, вынос 250 — зазор до радиаторов 110 мм), ковёр шерстяной 1400×2500 в зоне дивана (Т3), подушки 3 + 2 и плед на диван М-08 (Т4–Т6), пара постеров в дубовых рамах 600×800 над диваном (ДК1, ДК2; низ 1050), фикус в напольном кашпо в углу у окна 1 (ДК3), ваза на обеденном столе М-09 (ДК4). Спальня: римская штора с блэкаутом (Т7; в пол не идёт — слева внутренний блок КВ-2, под окном радиатор), ковёр 2000×3000 под кроватью (Т8), подушки 2 + 1 и плед на кровать М-12 (Т9–Т11), картина 1100×700 над изголовьем, зеркало в рост 600×1600 на стене В (ДК6), замиокулькас в углу (ДК7). Ванная: зеркало 450×650 над умывальником С-03 (ДК8). Санузел: постер 300×400 на стене В (ДК9). Прихожая: зеркало в рост 600×1700 на стене А слева от двери Д-2 (ДК10), постер 400×560 в простенке между дверями Д-2 и Д-3 (ДК11). Цвета — из палитры стиля: молочный, каменный, акценты — пыльный синий NCS S 4010-R90B и шалфей NCS S 3010-G10Y. Дорожка в прихожей не задана: весь пол — в зонах открывания пяти дверей. Знак «**» у позиций до подписи автора.	Не утверждено: подписи нет. решение исполнителя; предложение проектировщика, на утверждение А. С. Кырлана
ИЗ-5	12.11.2026	полный альбом	Разбор двух критиков по кадрам: мокрые зоны — «стерильный шоурум»: в ванной на полотенцесушителе С-04 нет полотенец, у ванны нет коврика, в санузле на полке короба инсталляции пусто (ИЗ-4 задал там только зеркало и постер).	Ванная: банные полотенца пыльного синего и ручные молочные на полотенцесушителе С-04 (Т12, Т13), коврик 800×450 у бортика ванны (Т14; вне полотна двери Д-4). Санузел: ваза с сухой веткой и свеча с диффузором на полке короба инсталляции С-05 (ДК12, ДК13). Смеситель ванны С-02 в данных задан («смеситель настенный») — правка не нужна. Прихожая не дополнялась: стены заняты дверями, щитами и домофоном, пол — в зонах открывания пяти дверей (см. ИЗ-4). Знак «**» у позиций до подписи автора.	Не утверждено: подписи нет. решение исполнителя; предложение проектировщика, на утверждение А. С. Кырлана

Примечания


1. Номера листов — по ведомости рабочих чертежей комплекта (лист «Общие данные»).
2. Графа «Если решения нет» показывает состояние решения на листах; влияние на сроки и стоимость по пунктам не оценивалось.
3. Пункт, по которому принято решение, при следующем выпуске комплекта из таблиц исключается.

	Лист	№ док.	Подпись	Дата	Проект: Квартира 58 м²			
Дизайнер	Кырлан А.С.			14.11.26	Открытые вопросы, принятые допущения и конфликты. Лист 2 из 2	Стадия	Лист	Листов
Проверил						П	72	92
Н. контр.								
Утв.								


Вид с фасадами (М 1:20)

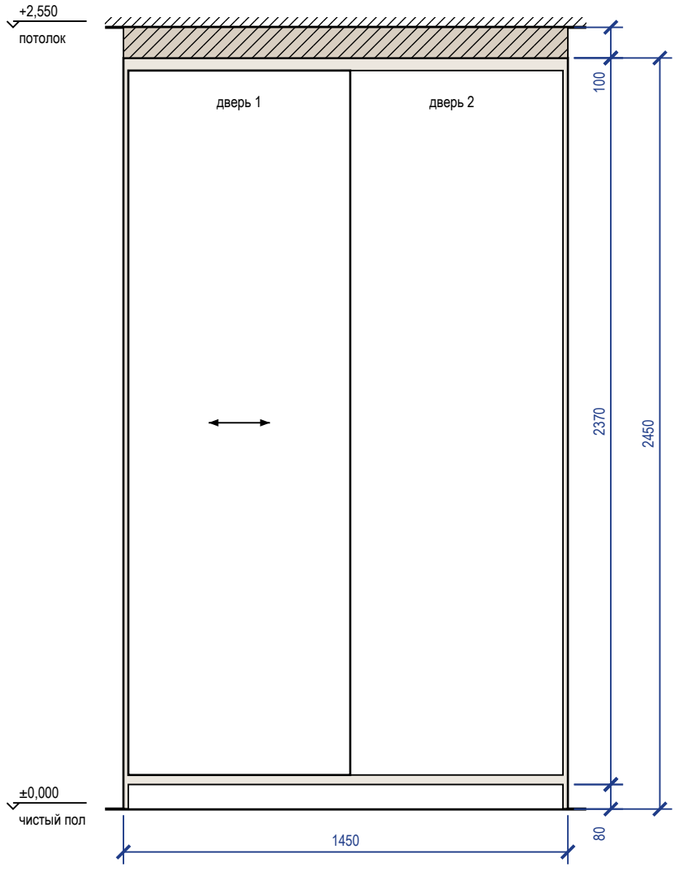


Вид без фасадов (М 1:20)

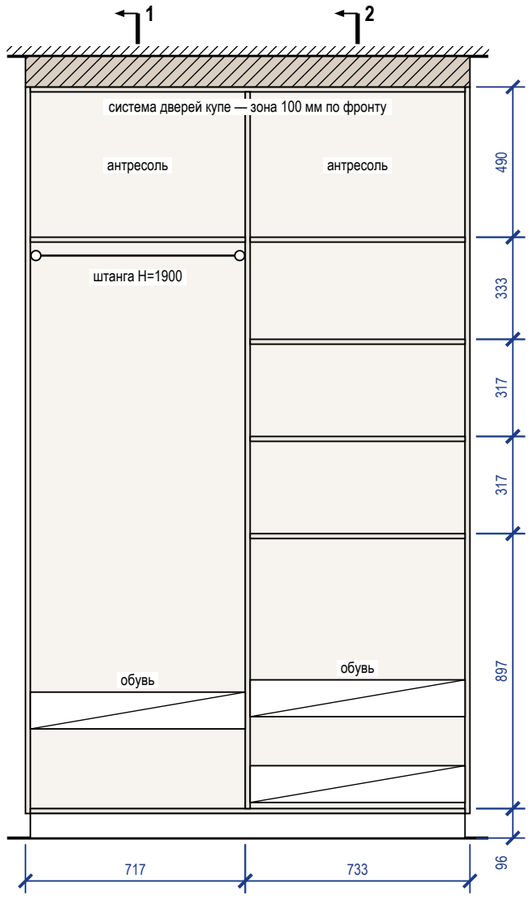

Разрез 1-1 (М 1:20)

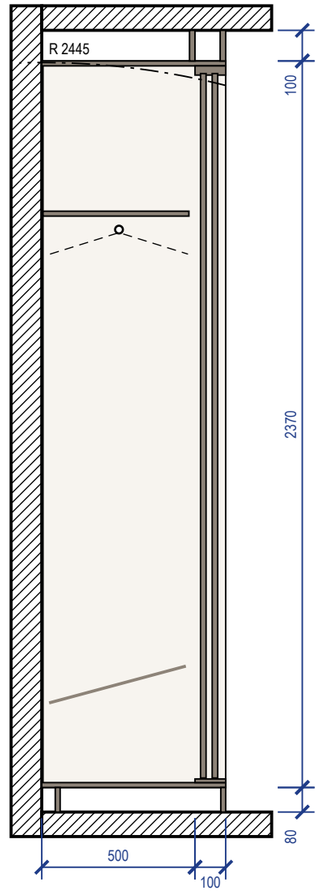


Разрез 2-2 (М 1:20)

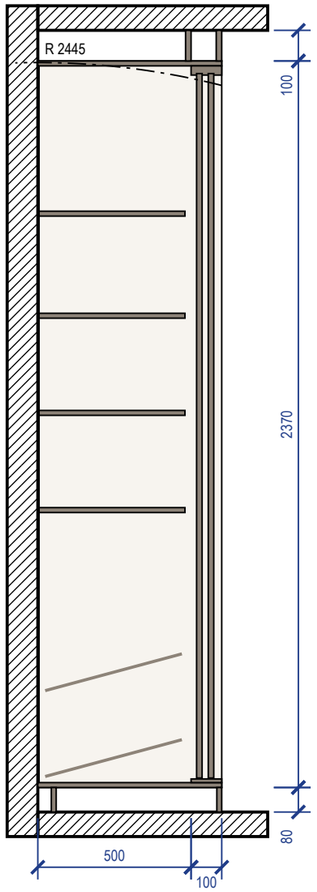

Примечания

1. Размеры — в мм по чистовой отделке; изделие 1450×600×2450 (Ш×Г×В). Перед раскроем — контрольный замер цеха после чистовой отделки стен, пола и потолка.
2. Корпус — ЛДСП 16 мм, задняя стенка ХДФ 4 мм в паз, цоколь 80 мм на регулируемых опорах; двери купе — ЛДСП 10 мм в алюминиевом профиле; нахлёст 30 мм, ширина двери 724 мм, высота — проём минус 40 мм; цвет — по колерной карте.
3. Кромка: скрытые торцы 0,4 мм, видимые 1 мм (ПВХ/АБС).
4. Номинальные зазоры: дверь купе — боковина 3 мм, фасад ящика — стойка 2 мм; ящики внутри купе — с накладкой 30 мм на стойке со стороны нахлёста дверей.
5. Присадка по 32-й системе — выполняет цех.
6. Компенсатор 100 мм — короб из ЛДСП по фронту и торцам, подгоняется к потолку при монтаже (припуск 20 мм), крепится к корпусу и к потолку.
7. Подъём корпуса: диагональ боковины без цоколя $\sqrt{(2370^2 + 600^2)} = 2445$ мм < 2550 мм до потолка — корпус собирается лёжа, поднимается поворотом и ставится на цоколь.
8. Крепление к стене от опрокидывания — уголки 2 шт. к несущему основанию (монтажная схема шкафов).

3D орто

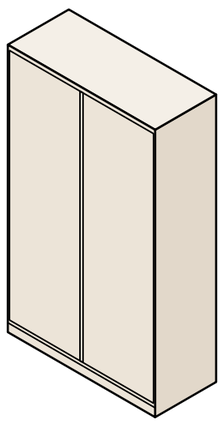


	Лист	№ док.	Подпись	Дата
Дизайнер	Кырлан А.С.			14.11.26
Проверил				
Н. контр.				
Утв.				

Проект: Квартира 58 м² — **М 1:20**


Шкаф-купе М-15	Стадия	Лист	Листов
	П	Д1	92

выпуск 14.11.2026 № 2b6bd7c078 · стр. 73 из 92


Общий вид (М 1:20)

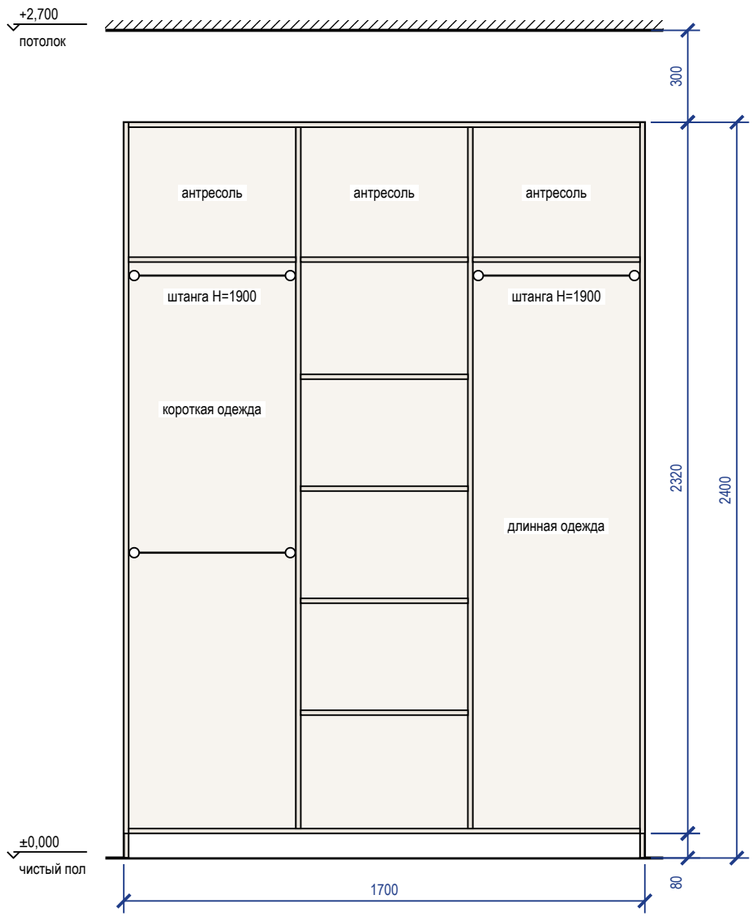


Наполнение, размеры в свету (М 1:20)

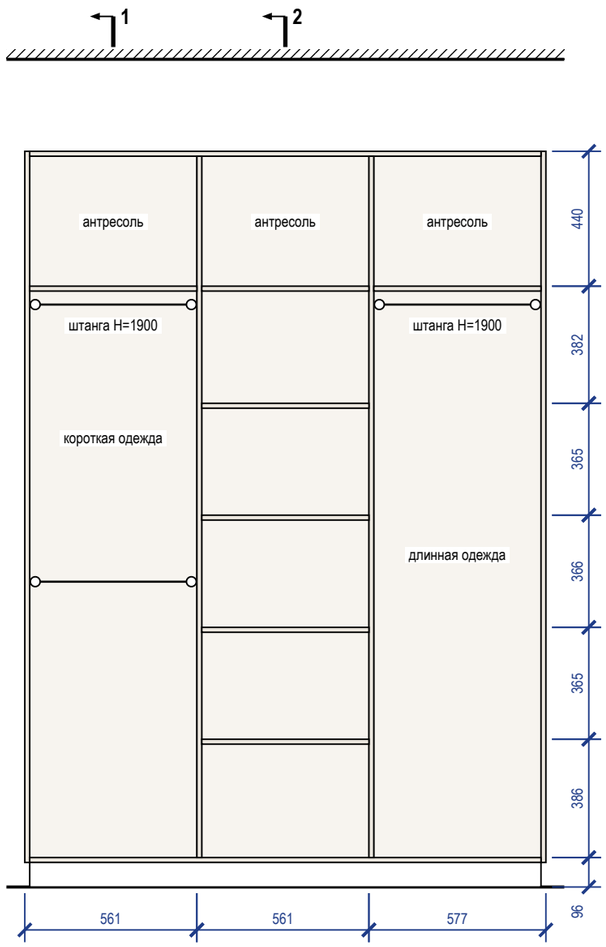

Разрез 1-1 (М 1:20)

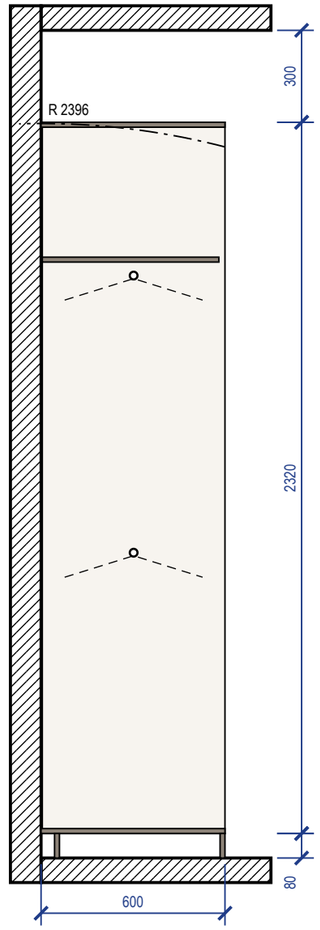


Разрез 2-2 (М 1:20)

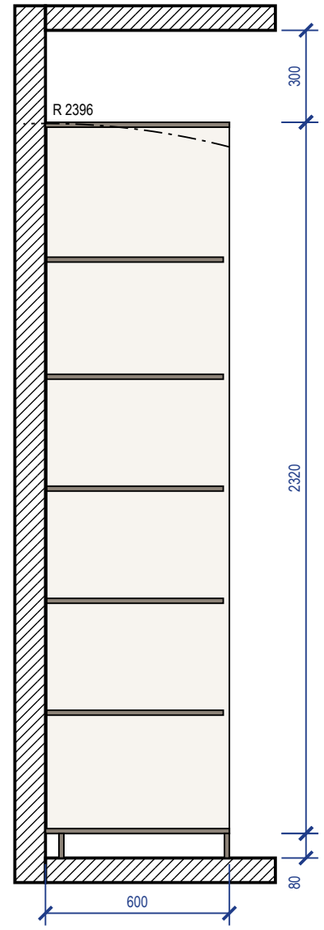

Примечания

1. Размеры — в мм по чистовой отделке; изделие 1700×600×2400 (Ш×Г×В). Перед раскроем — контрольный замер цеха после чистовой отделки стен, пола и потолка.
2. Корпус — ЛДСП 16 мм, задняя стенка ХДФ 4 мм в паз, цоколь 80 мм на регулируемых опорах; открытая система: без фасадов.
3. Кромка: скрытые торцы 0,4 мм, видимые 2 мм (ПВХ/АБС).
4. Присадка по 32-й системе — выполняет цех.
5. Зазор до потолка 300 мм.
6. Подъём корпуса: диагональ боковины без цоколя $\sqrt{(2320^2 + 600^2)} = 2396$ мм < 2700 мм до потолка — корпус собирается лёжа, поднимается поворотом и ставится на цоколь.
7. Крепление к стене от опрокидывания: крепление к стене, 3 точки; основание стены и шаг анкеров — монтажная схема шкафов.

3D орто

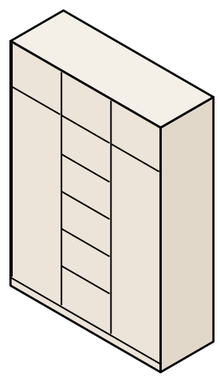

	Лист	№ док.	Подпись	Дата
Дизайнер	Кырлан А.С.			14.11.26
Проверил				
Н. контр.				
Утв.				


Проект: Квартира 58 м² — **М 1:20**

Система хранения М-16


Стадия	Лист	Листов
П	Д2	92

выпуск 14.11.2026 № 2b6bd7c078 · стр. 74 из 92


Вид с фасадами (М 1:25)

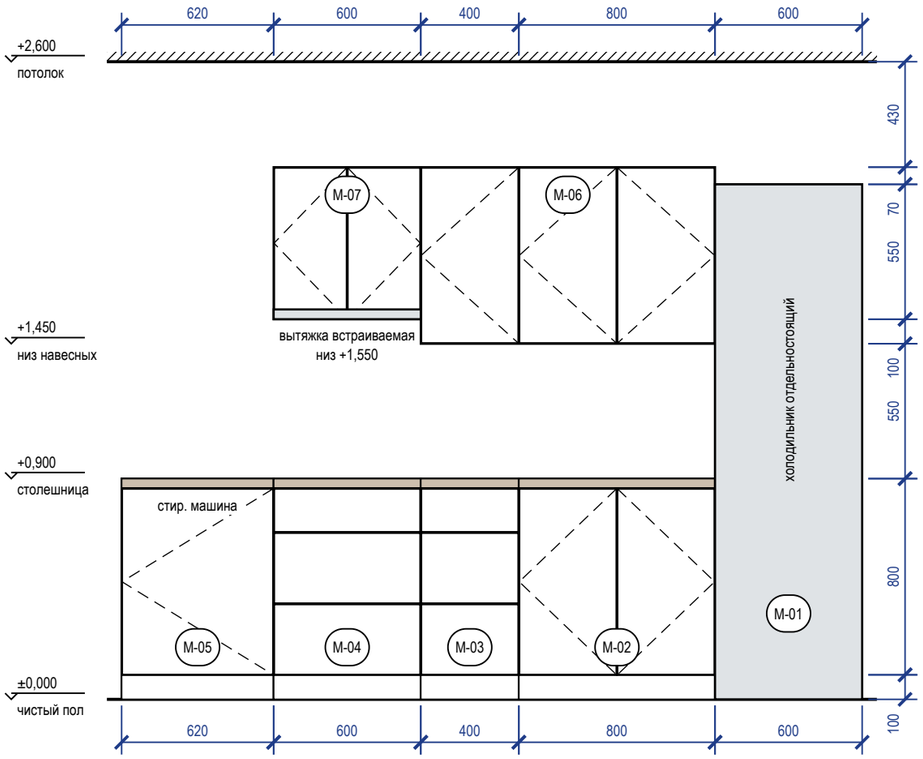


Вид без фасадов: наполнение, выводы (М 1:25)

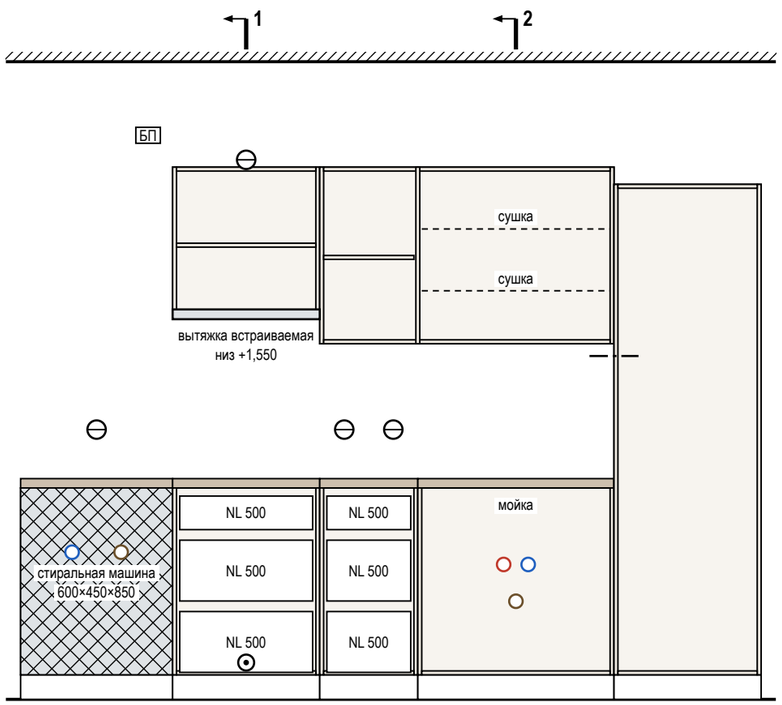


Разрез 1-1 (М 1:25)

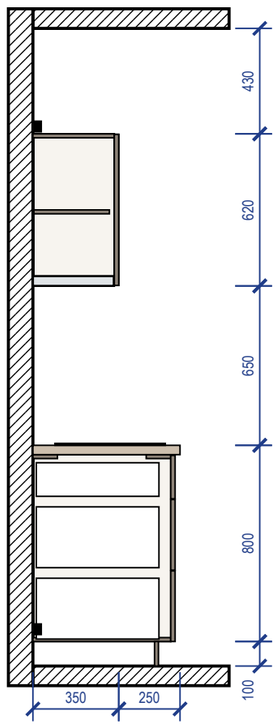

Разрез 2-2 (М 1:25)

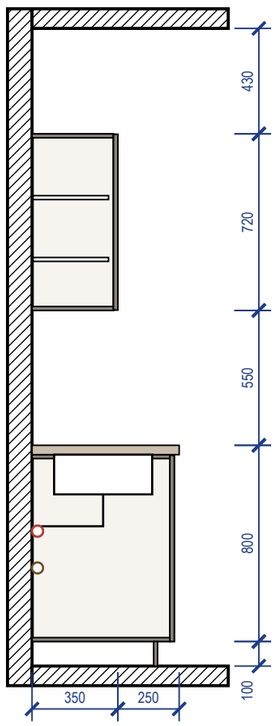

3D орто

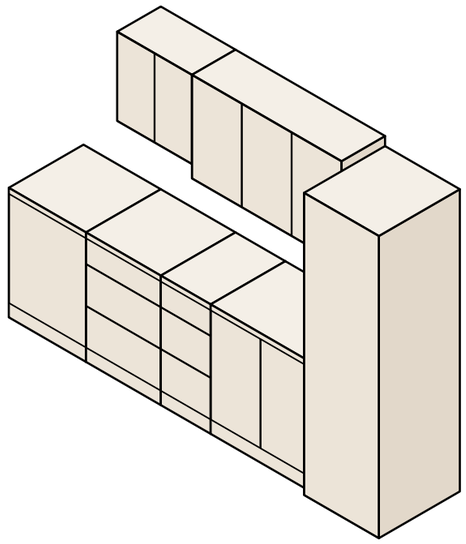

Примечания

1. Размеры — в мм по чистовой отделке, вид из помещения; марки — как на плане расстановки. Перед раскроем — контрольный замер цеха после фартука и пола.
2. Корпуса — ЛДСП 16 мм, задняя стенка ХДФ 4 мм; фасады — МДФ эмаль 18 мм, цвет по колерной карте; столешница 38 мм, свес 20 мм; цоколь 100 мм.
3. Кромка: скрытые торцы 0,4 мм, видимые 1 мм. Номинальные зазоры: между фасадами 3 мм, фасад — столешница 3 мм, фасад — стена не менее 3 мм.
4. Ящики полного выдвижения и петли — с доводчиком; присадка по 32-й системе — выполняет цех.
5. Наименования и габариты модулей (М…) — в ведомости изделий, лист 24.
6. Вытяжка встраивается в дно навесного модуля М-07 над варочной: её низ на 1550 мм от пола, 650 мм над панелью (не меньше 650 мм).
7. Ниши техники — по монтажным схемам выбранных моделей: решётка в цоколе и канал за пеналом холодильника, зазор за духовым шкафом, фасад ПММ на двери машины.

	Лист	№ док.	Подпись	Дата	Проект: Квартира 58 м²			М 1:25
Дизайнер	Кырлан А.С.			14.11.26	Кухня (пом. 1). Развёртка гарнитура	Стадия	Лист	Листов
Проверил						П	Д3	92
Н. контр.								
Утв.								

выпуск 14.11.2026 № 2b6bd7c078 · стр. 75 из 92

Ведомость отделки помещений (форма 1 прил. А ГОСТ 21.501-2018)

№	Наименование помещения	Потолок			Стены и перегородки			Низ стен (плинтус)			Пол		Примечание
		Вид отделки	Код цвета	S, м²	Вид отделки	Код цвета	S, м²	Вид отделки	Код цвета	L, м	Вид отделки	S, м²	
1	Кухня-гостиная 21,04 м²	ГКЛ по каркасу П113, отм. +2,600; +2,550; окраска, Tikkurila, глубокоматовая	NCS S 0300-N	21,04	Окраска, Tikkurila, полуматовая, подготовка Q3	NCS S 1002-Y50R	41,25	Плинтус МДФ h=110 мм, SX184	NCS S 0300-N	17,7	Аналог: инженерная доска, дуб натуральный, масло, 1-полосная, 14/4 мм, на клею; тип 1, отм. ЧП ±0,000	21,04	Н стен 2600 (до потолка)
2	Спальня 13,95 м²	ГКЛ по каркасу П113, отм. +2,600; +2,550; окраска, Tikkurila, глубокоматовая	NCS S 0300-N	13,95	Окраска, Tikkurila, глубокоматовая, подготовка Q3	NCS S 1502-Y50R	33,91	Плинтус МДФ h=110 мм, SX184	NCS S 0300-N	14,2	Аналог: инженерная доска, дуб натуральный, масло, 1-полосная, 14/4 мм, на клею; тип 1, отм. ЧП ±0,000	13,95	Н стен 2550 (до потолка)
3	Ванная 2,95 м²	ГКЛВ по каркасу П113, отм. +2,600; окраска, Tikkurila, глубокоматовая	NCS S 0300-N	2,95	Облицовка плиткой, 610015000370, 600×1200 мм, клей С2	Italon 610015000370	16,94	нет (облицовка от пола)			Керамогранит, SG651622R, 600×600 мм; тип 2, отм. ЧП −0,015	2,95	Н стен 2615 (до потолка); тёплый пол; гидроизоляция обмазочная, 2 слоя, с заведением на стены 200 мм; над ванной — до 2000 и 300 мм за борт (по пирогу пола); тест проливом и акт скрытых работ
4	Санузел 1,80 м²	ГКЛВ по каркасу П113, отм. +2,600; окраска, Tikkurila, глубокоматовая	NCS S 0300-N	1,80	Облицовка плиткой, 610015000370, 600×1200 мм, клей С2	Italon 610015000370	14,12	нет (облицовка от пола)			Керамогранит, SG651622R, 600×600 мм; тип 2, отм. ЧП −0,015	1,80	Н стен 2615 (до потолка); гидроизоляция обмазочная, 2 слоя, с заведением на стены 200 мм (по пирогу пола); тест проливом и акт скрытых работ
5	Прихожая 9,55 м²	ГКЛ по каркасу П113, отм. +2,550; +2,600; окраска, Tikkurila, глубокоматовая	NCS S 0300-N	9,55	Окраска, Tikkurila, полуматовая, подготовка Q3	NCS S 1502-Y50R	22,66	Плинтус МДФ h=110 мм, SX184	NCS S 0300-N	8,0	Керамогранит, SG651622R, 600×600 мм; тип 3, отм. ЧП ±0,000	9,55	Н стен 2550 (до потолка)
6	Гардеробная 5,94 м²	Существующий потолок, отм. +2,700; окраска, Tikkurila Anti-Reflex 2, глубокоматовая, 2 слоя, подготовка Q3	Tikkurila V503	5,94	Окраска, Tikkurila Harmony, матовая, 2 слоя, подготовка Q3	Tikkurila V503	24,67	Плинтус МДФ h=110 мм, SX184	Tikkurila V503	9,0	Аналог: инженерная доска, дуб натуральный, масло, 1-полосная, 14/4 мм, на клею; тип 1, отм. ЧП ±0,000	5,94	Н стен 2700 (до потолка); плинтус в цвет: стены
	Итого			**55,23**			**153,54**			**48,8**		**55,23**	

Сводка площадей по материалам отделки

Поверхность	Материал / код цвета	Серия	Площадь, м²
Потолок	NCS S 0300-N		49,29
Потолок	Tikkurila V503	Anti-Reflex 2	5,94
Стены	NCS S 1002-Y50R		41,25
Стены	NCS S 1502-Y50R		56,57
Стены	облицовка плиткой 600×1200 мм, Italon 610015000370	610015000370	31,05
Стены	Tikkurila V503	Harmony	24,67

Примечания

1. Площади поверхностей — по чистым граням стен до отделки: стены = периметр × высоту от чистого пола помещения до низа потолка минус проёмы (облицовка плиткой — до верха облицовки); плинтус = периметр минус дверные проёмы; пол и потолок — по площади помещения. Количество плиток по раскладке. Площади помещений — с учётом всех частей помещения; откосы в площадь стен не входят.
2. Акцентные стены — отдельными строками, их площадь вычтена из основной отделки стен помещения.
3. Плинтус — длина по периметру за вычетом дверных проёмов; примыкания к наличникам и встроенной мебели — по развёрткам.
4. Формат плитки — Ш×В×Т (ширина × высота в положении укладки × толщина), мм; на полу — вдоль стен А/В × вдоль стен Б/Г.
5. Коды цвета — по веерам производителей; колеровка каждой краски одной партией, проверка выкраса при свете D65 и при лампах проекта.
6. Уровни подготовки Q1–Q4 — система Knauf, не норма ГОСТ/СП; допуски поверхностей — по СП 71.13330.2017 (действующая редакция).
7. «аналог:» — изделие задано характеристиками, марку и артикул согласовать с заказчиком до закупки.

	Лист	№ док.	Подпись	Дата	Проект: Квартира 58 м²			
Дизайнер	Кырлан А.С.			14.11.26	Ведомость отделки помещений	Стадия	Лист	Листов
Проверил						П	С1	92
Н. контр.								
Утв.								

Поз.	Наименование и техническая характеристика	Тип, марка, обозначение документа	Код продукции	Поставщик	Ед. изм.	Кол.	Образец	Примечание
	Лакокрасочные материалы							
1	Краска интерьерная водно-дисперсионная акриловая для стен, полуматовая, класс мокрого истирания 1 по EN 13300, база A; цвет NCS S 1002-Y50R, колеровка машинная	Tikkurila		Tikkurila	л	11,7		поз. К1 колерной карты; пом. 1; S = 41,2 м² × 2 сл. × 0,12 л/м² = 9,9 л, +10 % и 0,5 л на подкраску → ≥ 11,4 л; тара 1 × 9 л + 1 × 2,7 л
2	Краска интерьерная водно-дисперсионная для потолков, глубокоматовая, класс мокрого истирания 1 по EN 13300, база A; цвет NCS S 0300-N, колеровка машинная	Tikkurila		Tikkurila	л	9,9		поз. К2 колерной карты; пом. 1, 3, 4, 5; S = 35,3 м² × 2 сл. × 0,12 л/м² = 8,5 л, +10 % и 0,5 л на подкраску → ≥ 9,8 л; тара 1 × 9 л + 1 × 0,9 л
3	Краска интерьерная водно-дисперсионная акриловая для стен, глубокоматовая, класс мокрого истирания 2 по EN 13300, база A; цвет NCS S 1502-Y50R, колеровка машинная	Tikkurila		Tikkurila	л	9,9		поз. К4 колерной карты; пом. 2; S = 33,9 м² × 2 сл. × 0,12 л/м² = 8,1 л, +10 % и 0,5 л на подкраску → ≥ 9,5 л; тара 1 × 9 л + 1 × 0,9 л
4	Краска интерьерная водно-дисперсионная для потолков, глубокоматовая, класс мокрого истирания 2 по EN 13300, база A; цвет NCS S 0300-N, колеровка машинная	Tikkurila		Tikkurila	л	4,5		поз. К5 колерной карты; пом. 2; S = 13,9 м² × 2 сл. × 0,12 л/м² = 3,3 л, +10 % и 0,5 л на подкраску → ≥ 4,2 л; тара 1 × 2,7 л + 2 × 0,9 л
5	Краска интерьерная водно-дисперсионная акриловая для стен, полуматовая, класс мокрого истирания 1 по EN 13300, база A; цвет NCS S 1502-Y50R, колеровка машинная	Tikkurila		Tikkurila	л	7,2		поз. К6 колерной карты; пом. 5; S = 22,7 м² × 2 сл. × 0,12 л/м² = 5,4 л, +10 % и 0,5 л на подкраску → ≥ 6,5 л; тара 2 × 2,7 л + 2 × 0,9 л
6	Краска интерьерная водно-дисперсионная акриловая для стен, матовая, класс мокрого истирания 1 по EN 13300, база A; цвет по вееру Tikkurila V503 «Winter», колеровка машинная	Tikkurila Harmony		Tikkurila	л	7,2		поз. К7 колерной карты; пом. 6; S = 24,7 м² × 2 сл. × 0,12 л/м² = 5,9 л, +10 % и 0,5 л на подкраску → ≥ 7,0 л; тара 2 × 2,7 л + 2 × 0,9 л
7	Краска интерьерная водно-дисперсионная акриловая для потолков, глубокоматовая, класс мокрого истирания 2 по EN 13300, база A; цвет по вееру Tikkurila V503 «Winter», колеровка машинная	Tikkurila Anti-Reflex 2		Tikkurila	л	2,7		поз. К8 колерной карты; пом. 6; S = 5,9 м² × 2 сл. × 0,12 л/м² = 1,4 л, +10 % и 0,5 л на подкраску → ≥ 2,1 л; тара 1 × 2,7 л
8	Акрил, полуматовая в цвет NCS S 0300-N — окраска плинтуса	аналог по характеристикам			л	1,4		поз. К3; пом. 1, 2, 5; L = 39,9 м, S = 5,0 м² × 2 сл. × 0,12 л/м² + 10 %; продукт подобрать в веере NCS
9	Краска для МДФ и дерева в цвет Tikkurila V503 «Winter» — окраска плинтуса; блеск не ниже блеска стен	марка не задана			л	0,5		поз. К9; пом. 6; L = 9,0 м, S = 1,1 м² × 2 сл. × 0,12 л/м² + 10 %; продукт подобрать в веере Tikkurila
10	Грунтовка акриловая под окраску стен и потолков — из системы производителя краски	по системе краски			м²	178		площадь окраски стен, акцентов и потолков; 1 слой перед окраской; расход — по ТУ грунтовки
	Плитка и керамогранит							
11	SG651622R, 600×600 мм, противоскольжение R10	SG651622R		Kerama Marazzi	м²	19,44		шов 2 мм; Ванная, пол; Санузел, пол; Прихожая, пол; по раскладке 48 шт (S = 14,30 м²), с запасом 54 шт
12	610015000370, 1200×600 мм	610015000370		Italon	м²	70,56		шов 2 мм; Ванная, стены А–Г; Ванная, короб стояков Ш1 489×319; Санузел, стены А–Г; Санузел, короб инсталляции; по раскладке 87 шт (S = 31,81 м²), с запасом 98 шт
	Напольные покрытия							
13	Инженерная доска, дуб натуральный, масло, 1-полосная, 14/4 мм, класс 33, эмиссия E1, укладка на клей	аналог по характеристикам			м²	37,6		пом. 1, 2; S = 35,12 м² (пол + половина стены в дверных проёмах, как в смете) + 7 %; к заказу — кратно упаковке
14	Инженерная доска, дуб натуральный, масло, 1-полосная, 14/4 мм, эмиссия E1, укладка на клей	аналог по характеристикам			м²	6,4		пом. 6; S = 5,96 м² (пол + половина стены в дверных проёмах, как в смете) + 7 %; к заказу — кратно упаковке
15	Клей для паркета и инженерной доски, эластичный (СМП / полиуретановый)	по рекомендации производителя доски			м²	42		площадь приклейки; расход и шпатель — по ТУ клея
	Погонажные изделия							
16	SX184, h = 110 мм, крепление к стене, окраска в цвет NCS S 0300-N	SX184		Orac Decor	м	44		пом. 1, 2, 5; L = 39,9 м (периметр без дверных проёмов) + 10 % на подрезку; в штуках — по длине планки
17	SX184, h = 110 мм, крепление к стене, окраска в цвет Tikkurila V503	SX184		Orac Decor	м	10		пом. 6; L = 9,0 м (периметр без дверных проёмов) + 10 % на подрезку; в штуках — по длине планки
	Смеси и материалы для облицовки							
18	Затирка для швов плитки	аналог по характеристикам			кг	3,9		по раскладке (a+b)/(a·b) × шов × t × 1,6 + 10 %
19	Клей плиточный C2 S1 по EN 12004, слой 5 мм	аналог по характеристикам			кг	28		2 меш. по 25 кг; 1,5 кг/м² на 1 мм слоя + 10 %
20	Клей плиточный C2 по EN 12004, слой 5 мм	аналог по характеристикам			кг	266		11 меш. по 25 кг; 1,5 кг/м² на 1 мм слоя + 10 %
21	Гидроизоляция обмазочная мокрых зон: пол, стены по периметру, зоны замачивания; 2 слоя с армирующей лентой в углах	аналог по характеристикам			м²	7,8		площадь по листу раскладки плитки + 10 %; расход смеси — по ТУ
22	Лента демпферная по периметру пола из плитки	аналог по характеристикам			м	21		периметр без дверных проёмов + 10 %

Примечания

1. Количества — из геометрии проекта: площади поверхностей по чистым граням стен до отделки (те же, что в ведомости отделки и колерной карте), плитка, клей и затирка — по раскладке плиточника; в графе «Кол.» — к заказу, с запасом.
2. Краска: расход 0,12 л/м² на слой в 2 слоя, если по ТУ не задан иной; запас 10 % и 0,5 л на подкраску каждого кода. Один код — одна партия, колеровка машинная в колеровочном центре бренда; в заказ — только после утверждения выкраса (колерная карта). Фасовка — по каталогу бренда на дату выпуска; к заказу — не меньше расчётного объёма.
3. «Аналог по характеристикам» — допускается изделие другого производителя с характеристиками не ниже указанных, по согласованию с автором проекта.
4. Графы «Код продукции» и «Масса 1 ед.» не заполнены: коды по классификатору продукции не присвоены, масса единицы до 25 кг (ГОСТ 21.110-2013).
5. Грунтовка и клей для доски указаны площадью обработки; объём — по ТУ выбранного продукта.

	Лист	№ док.	Подпись	Дата	Проект: Квартира 58 м²			
Дизайнер	Кырлан А.С.			14.11.26	Спецификация отделочных материалов	Стадия	Лист	Листов
Проверил						П	С2	92
Н. контр.								
Утв.								

выпуск 14.11.2026 № 2b6bd7c078 · стр. 77 из 92

Список покупок: материалы для магазина

№	Что купить	Артикул или характеристика	Нужно с запасом	Брать в магазине	Фасовка	Уточнить в магазине	Помещения	Кто покупает
Покрытия полов и облицовка								
1	Инженерная доска (дуб натуральный, рабочий слой 4 мм, эмиссия E1, прямая укладка)	по характеристике: инженерная доска, дуб натуральный, масло, 1-полосная, 14/4 мм	43,96 м²	44 м²		уточнить в магазине: м² в упаковке	1, 2, 6	по проекту
2	Клей для паркетной и инженерной доски (эластичный, по ТУ изготовителя доски)	на выбор бригады по проекту	41,08 м²			уточнить в магазине: расход и фасовку — по выбранному продукту		бригада
3	Керамогранит 600×600 мм SG651622R	SG651622R	53 шт	54 шт		уточнить в магазине: штук в коробке	3, 4, 5	по проекту
4	Керамогранит 1200×600 мм 610015000370	610015000370	96 шт	98 шт		уточнить в магазине: штук в коробке	3, 4	по проекту
Сухие смеси и гидроизоляция								
5	Клей плиточный цементный класса C2 S1 (ГОСТ Р 56387-2018)	на выбор бригады по проекту	27,43 кг	2 меш.	мешок 25 кг			по проекту
6	Клей плиточный цементный класса C2 (ГОСТ Р 56387-2018)	на выбор бригады по проекту	265,03 кг	11 меш.	мешок 25 кг			по проекту
7	Затирка цементная класса класс не задан, цвет — по колерной карте	на выбор бригады по проекту	3,86 кг	2 упак.	упак. 2 кг			по проекту
8	Гидроизоляция обмазочная полимерная, 2 слоя, лента в углах, манжеты на выводах	на выбор бригады по проекту	7,78 м²			уточнить в магазине: расход и фасовку — по выбранному продукту	3, 4	бригада
9	Лента демпферная по периметру пола из плитки	на выбор бригады по проекту	21,05 м	22 м		уточнить в магазине: фасовку		бригада
10	Смесь цементно-песчаная для стяжки М200 (50 мм, 33 мм)	на выбор бригады по проекту	2,85 м³			уточнить в магазине: расход и фасовку — по выбранному продукту		бригада
11	Смесь штукатурная гипсовая для машинного и ручного нанесения по маякам, слой до 10 мм	на выбор бригады по проекту	27,14 м²			уточнить в магазине: расход и фасовку — по выбранному продукту	6	бригада
Короба из ГКЛВ								
12	Лист ГКЛВ 12,5 мм, 2500 × 1200 мм, обшивка коробов в 2 слоя	на выбор бригады по проекту	4,64 м²	2 лист.	лист 3,00 м²		3	бригада
13	Профиль стальной оцинкованный 27 × 28 мм: каркас коробов (стойки и направляющие)	на выбор бригады по проекту	13,29 м	5 шт	хлыст 3 м			бригада
Слаботочные сети								
14	Кабель домофона — тип по системе поставщика	на выбор бригады по проекту	3,4 м	4 м		уточнить в магазине: длину бухты		бригада
15	Кабель коаксиальный RG-6 (75 Ом) к розеткам ТВ	на выбор бригады по проекту	16,3 м	17 м		уточнить в магазине: длину бухты		бригада
16	Кабель U/UTP кат. 5e (LAN, Wi-Fi и камеры по PoE)	на выбор бригады по проекту	30,1 м	31 м		уточнить в магазине: длину бухты		бригада
17	Гофротруба Ø20 для слаботочных линий, отдельно от силовых	на выбор бригады по проекту	44,8 м	45 м		уточнить в магазине: длину бухты		бригада
18	Розетка компьютерная RJ45, кат. 6, с рамкой и подрозетником	на выбор бригады по проекту	2 шт	2 шт	шт			бригада

	Лист	№ док.	Подпись	Дата	Проект: Квартира 58 м²			
Дизайнер	Кырлан А.С.			14.11.26				
Проверил					Список покупок	Стадия	Лист	Листов
Н. контр.								
Утв.						П	С3	92

выпуск 14.11.2026 № 2b6bd7c078 · стр. 78 из 92

Список покупок: материалы для магазина (продолжение)

№	Что купить	Артикул или характеристика	Нужно с запасом	Брать в магазине	Фасовка	Уточнить в магазине	Помещения	Кто покупает
19	Розетка телевизионная (коаксиальная) с рамкой и подрозетником	на выбор бригады по проекту	1 шт	1 шт	шт			бригада
20	Трубка или монитор домофона (поставка домофонной организации)	на выбор бригады по проекту	1 шт	1 шт	шт			по проекту
21	Щит слаботочный ЩС: корпус, DIN-рейка, розетки 220 В	на выбор бригады по проекту	1 шт	1 шт	шт			бригада
22	Патч-панель, портов не менее 2	на выбор бригады по проекту	1 шт	1 шт	шт			бригада
Лакокрасочные материалы								
23	Краска интерьерная акриловая, полуматовая, класс истирания 1	Tikkurila S 1002-Y50R	10,89 л	5 банк.	банка 2,7 л		1	по проекту
24	Краска интерьерная водно-дисперсионная, глубокоматовая, класс истирания 1	Tikkurila S 0300-N	13,01 л	5 банк.	банка 2,7 л		1, 2, 3, 4, 5	по проекту
25	Краска интерьерная акриловая, глубокоматовая, класс истирания 2	Tikkurila S 1502-Y50R	8,95 л	4 банк.	банка 2,7 л		2	по проекту
26	Краска интерьерная акриловая, полуматовая, класс истирания 1	Tikkurila S 1502-Y50R	5,98 л	3 банк.	банка 2,7 л		5	по проекту
27	Краска интерьерная акриловая, матовая, класс истирания 1	Tikkurila Harmony V503 «Winter»	6,51 л	3 банк.	банка 2,7 л		6	по проекту
28	Краска интерьерная акриловая, глубокоматовая, класс истирания 2	Tikkurila Anti-Reflex 2 V503 «Winter»	1,57 л	1 банк.	банка 2,7 л		6	по проекту
29	Шпаклёвка финишная полимерная под окраску (стены и потолки, Q3)	на выбор бригады по проекту	195,49 м²			уточнить в магазине: расход и фасовку — по выбранному продукту		бригада
30	Грунтовка акриловая глубокого проникновения, 2 слоя	на выбор бригады по проекту	229,66 м²			уточнить в магазине: расход и фасовку — по выбранному продукту		бригада
Погонажные изделия и потолки								
31	Плинтус напольный МДФ под покраску, h=110 мм, крепление к стене	SX184	53,7 м.п.	23 шт	хлыст 2,4 м		1, 2, 5, 6	по проекту
32	Потолок подвесной ГКЛ/ГКЛВ по каркасу Knauf П113: листы, профили, подвесы, лента, шпаклёвка швов	Knauf П113	49,29 м²		комплект	уточнить в магазине: расход и фасовку — по выбранному продукту		по проекту

Примечания

1. «Нужно с запасом» — расход по чертежам и раскладке плюс запас на подрезку и подкраску; «Брать в магазине» — то же количество в единицах, которыми продают (банки, мешки, упаковки, листы, штуки, литры).
2. «Уточнить в магазине» — фасовки этого товара в проекте нет: спросите у продавца, сколько в упаковке, и возьмите целое число упаковок не меньше «Нужно с запасом».
3. Плитку, доску и краску одного цвета берите одной партией (один калибр и тон на помещение) и сохраните чек и номер партии до конца ремонта.
4. «По характеристике» — артикул не выбран: подойдёт любой товар с этими свойствами, согласуйте его с дизайнером до покупки. «Бригада» материал выбирает и закупает бригада по своей технологии.
5. Помещения: 1 — Кухня-гостиная; 2 — Спальня; 3 — Ванная; 4 — Санузел; 5 — Прихожая; 6 — Гардеробная; «—» — материал для нескольких помещений, расход по месту.

	Лист	№ док.	Подпись	Дата	Проект: Квартира 58 м²			
Дизайнер	Кырлан А.С.			14.11.26	Список покупок (окончание)	Стадия	Лист	Листов
Проверил						П	С4	92
Н. контр.								
Утв.								

выпуск 14.11.2026 № 2b6bd7c078 · стр. 79 из 92

Смета проекта: весь проект по категориям (прайсы собраны 21.09.2026, часть расценок сверена повторно 08.11.2026)

Категория	Позиций	С ценой	По КП	Сумма по позициям с ценой, ₽
Ремонт: работы	51	32	19	656 514
Ремонт: материалы отделки и черновые	27	12	15	586 098
Электрика: кабель, механизмы, щит	31	0	31	
Сантехника: приборы, трубы, арматура	34	0	34	
Доставка и услуги	4	1	3	58 610
Мебель (включая кухню)	14	0	14	
Свет: светильники и ленты	17	0	17	
Техника	4	0	4	
Декор и текстиль	35	0	35	
ИТОГО по позициям с ценой (цены — нижняя граница открытых прайсов)	**217**	**45**	**172**	**1 301 222**
Резерв на непредвиденные работы и материалы, 15 % от ремонта				195 183
ВЕСЬ ПРОЕКТ — вилка «от … до …», ₽				**1 301 222 … 1 496 405**
Позиции «по КП» — цена не названа, в итог НЕ входят: работы — 19; материалы отделки и черновые — 15; электрика: кабель, механизмы, щит — 31; сантехника: приборы, трубы, арматура — 34; доставка и услуги — 3; мебель (включая кухню) — 14; свет: светильники и ленты — 17; техника — 4; декор и текстиль — 35			**172**	**итог выше на их цену**

По этапам

Этап	Поз.	С ценой	Сумма, ₽
Демонтаж и черновые работы (работы)	10	5	121 170
Инженерные системы (работы)	23	11	76 266
Чистовые работы (работы)	18	16	459 078
Черновые материалы (смеси, ГКЛ, гидроизоляция)	13	2	23 400
Электрика: кабель, механизмы, щит, слаботочка	31	0	
Сантехника: приборы, трубы, арматура	34	0	
Чистовые материалы (отделка, двери)	14	10	562 698
Доставка и услуги	4	1	58 610
Резерв на непредвиденное, 15 %	1	1	195 183
Итого ремонт (с резервом)			**1 496 405**

По помещениям

Помещение	Работы, ₽	Материалы, ₽	Всего, ₽
Общее по объекту (без привязки к помещению)	8 262		8 262
1. Кухня-гостиная	186 799	130 068	316 867
2. Спальня	129 064	89 125	218 189
3. Ванная	78 198	160 593	238 791
4. Санузел	63 083	134 356	197 439
5. Прихожая	116 424	27 418	143 842
6. Гардеробная	74 684	44 538	119 222
Доставка и услуги			58 610
Резерв 15 %			195 183
Итого ремонт (с резервом)			**1 496 405**

Работы по этапам с расценками (ориентир)

№	Работа	Ед.	Объём	Расценка, ₽	Сумма, ₽	Расценка	Чей подряд
1. Демонтаж и черновые работы — работы, ориентир по открытым прайсам							
1	Демонтаж существующего покрытия пола до основания	м²	55,23	по КП			бригада
2	Демонтаж существующей отделки стен до основания	м²	153,55	по КП			бригада
3	Демонтаж существующей отделки потолка до основания	м²	55,23	по КП			бригада

	Лист	№ док.	Подпись	Дата	Проект: Квартира 58 м²			
Дизайнер	Кырлан А.С.			14.11.26				
Проверил					Смета проекта: этапы, помещения, итог	Стадия	Лист	Листов
Н. контр.						П	С5	92
Утв.								

выпуск 14.11.2026 № 2b6bd7c078 · стр. 80 из 92

Работы по этапам с расценками (ориентир) (продолжение)

№	Работа	Ед.	Объём	Расценка, ₽	Сумма, ₽	Расценка	Чей подряд
4	Демонтаж существующих дверных блоков	шт	6,00	по КП			бригада
5	Демонтаж существующих сантехприборов и электрооборудования (если есть)	компл		по КП			бригада
6	Устройство стяжки: стяжка ЦПС М200, 50 мм	м²	55,81	530	29 579	Ц1	бригада
7	Гидроизоляция обмазочная, 2 слоя: пол, стены на 200 мм, зоны замачивания	м²	7,07	450	3 182	Ц1	бригада
8	Штукатурка стен по маякам, до 10 мм	м²	24,67	530	13 075	Ц1	бригада
9	Штукатурка оконных откосов шириной до 200 мм	м²	2,59	540	1 399	Ц4	бригада
10	Потолок ГКЛ по каркасу П113, 1 слой	м²	49,29	1 500	73 935	Ц1	бригада
2. Инженерные системы — работы, ориентир по открытым прайсам							
11	Прокладка слаботочной линии: Кабель домофона — тип по системе поставщика, отдельно от силовых	м	3,40	по КП			бригада
12	Прокладка слаботочной линии: Кабель коаксиальный RG-6 (75 Ом) к розеткам ТВ, отдельно от силовых	м	16,30	по КП			бригада
13	Прокладка слаботочной линии: Кабель U/UTP кат. 5e (LAN, Wi-Fi и камеры по PoE), отдельно от силовых	м	30,10	по КП			бригада
14	Прокладка гофротрубы Ø20 для слаботочных линий, отдельно от силовых	м	44,80	140	6 272	Ц3	бригада
15	Сборка слаботочного щита ЩС: корпус, патч-панель, подключение линий и питания 220 В; коммутатор и точки доступа — оборудование заказчика	шт	1,00	по КП			бригада
16	Электроточка: подрозетник в бетоне, розетка, выключатель, вывод	шт	33,00	950	31 350	Ц3	бригада
17	Штробы в стенах под спуски кабеля к точкам — выполняются только после технического заключения о несущих стенах	м	59,00	по КП			бригада
18	Установка встраиваемого точечного светильника	шт	4,00	750	3 000	Ц3	бригада
19	Монтаж светильника: потолочного, подвесного, настенного	шт	8,00	1 200	9 600	Ц3	бригада
20	Монтаж LED-ленты в алюминиевый профиль	м	1,80	230	414	Ц3	бригада
21	Установка блока питания LED в доступном месте (люк, шкаф)	шт	2,00	570	1 140	Ц3	бригада
22	Установка автономного пожарного извещателя	шт	3,00	по КП			бригада
23	Сборка щита: установка автоматов и АВДТ групп, вводного автомата	шт	7,00	230	1 610	Ц3	бригада
24	Установка вводного УЗО	шт	1,00	380	380	Ц3	бригада
25	Монтаж инсталляции, установка подвесного унитаза и кнопки смыва	шт	1,00	10 500	10 500	Ц1	бригада
26	Короб инсталляции: каркас и обшивка ГКЛВ в 2 слоя, ревизионный доступ к смыву	шт	1,00	по КП			бригада
27	Короб стояков Ш1 489 × 319 мм (внутренний 436 × 266): каркас и обшивка ГКЛВ в 2 слоя, ревизионный люк 300 × 400	м²	2,11	по КП			бригада
28	Короб К1 над чистым полом: каркас и обшивка ГКЛВ под плитку (материалы — в спецификации ВК)	м	1,46	по КП			бригада
29	Установка ванны с сифоном	шт	1,00	6 000	6 000	Ц1	бригада
30	Установка умывальника (мойки) с сифоном и смесителем	шт	2,00	3 000	6 000	Ц1	бригада
31	Подключение стиральной (посудомоечной) машины к ВК	шт	1,00	по КП			бригада
32	Установка радиатора с узлом подключения и терморегулятором	шт	3,00	по КП			бригада
33	Монтаж сплит-системы КВ-1: внутренний блок на стене, трасса фреона и дренажа до наружного блока, вакуумирование, пусконаладка; наружный блок в корзине на фасаде (высотные работы)	шт	2,00	по КП			бригада
3. Чистовые работы — работы, ориентир по открытым прайсам							
34	Облицовка стен керамогранитом 1200×600 на клею	м²	28,35	2 500	70 875	Ц5	бригада

	Лист	№ док.	Подпись	Дата	Проект: Квартира 58 м²			
Дизайнер	Кырлан А.С.			14.11.26	Смета проекта: этапы, помещения, итог (продолжение)	Стадия	Лист	Листов
Проверил						П	С6	92
Н. контр.								
Утв.								

выпуск 14.11.2026 № 2b6bd7c078 · стр. 81 из 92

Работы по этапам с расценками (ориентир) (продолжение)

№	Работа	Ед.	Объём	Расценка, ₽	Сумма, ₽	Расценка	Чей подряд
35	Облицовка короба инсталляции (ГКЛВ) керамогранитом: лицо, боковины, полка	м²	3,46	2 500	8 650	Ц5	бригада
36	Укладка керамогранита на пол, 600×600, на клею	м²	14,73	1 800	26 514	Ц2	бригада
37	Затирка швов керамогранита	м²	46,11	150	6 917	Ц2	бригада
38	Грунтование стен, 2 слоя (под штукатурку и под отделку)	м²	153,55	96	14 741	Ц4	бригада
39	Шпаклёвка стен под окраску, 2 слоя (старт и финиш), уровень Q3	м²	122,49	750	91 868	Ц1	бригада
40	Грунтование и шпаклёвка оконных откосов, 2 слоя	м	14,40	300	4 320	Ц4	бригада
41	Грунтование потолка, 2 слоя	м²	55,23	96	5 302	Ц4	бригада
42	Шпаклёвка потолка под окраску, 2 слоя, уровень Q3	м²	55,23	950	52 469	Ц1	бригада
43	Окраска потолка водно-дисперсионной краской, 2 слоя	м²	55,23	360	19 883	Ц1	бригада
44	Окраска стен водно-дисперсионной краской, 2 слоя	м²	145,50	300	43 650	Ц1	бригада
45	Окраска оконных откосов, 2 слоя	м	14,40	120	1 728	Ц4	бригада
46	Укладка инженерной доски на клей	м²	41,08	1 200	49 296	Ц1	бригада
47	Установка плинтуса МДФ h=110 мм	м	48,82	450	21 969	Ц1	бригада
48	Окраска плинтуса в тоне S 0300-N, 2 слоя	м	48,82	300	14 646	Ц1	бригада
49	Монтаж дверей скрытого монтажа под покраску (поставщик дверей)	шт	5,00	5 250	26 250	Ц1	поставщик
50	Входная дверь, поставка с монтажом и откосами	шт	1,00	по КП			поставщик
51	Монтаж телевизора ОБ-01 на кронштейн, скрытая прокладка HDMI и питания (штроба, трубка), подключение акустики	шт	1,00	по КП			бригада
4. Прочие работы и услуги — работы, ориентир по открытым прайсам							
52	Кухонный гарнитур по проекту кухни, изготовление и монтаж (4–8 нед.)	компл	1,00	по КП			поставщик
	Итого работы (позиции с расценкой)				**656 514**		

Примечания

1. Итог «ВЕСЬ ПРОЕКТ» — не прогноз, а сумма того, у чего есть цена: ремонт (работы и материалы по смете сметчика), мебель, свет, техника и декор — по ценам из данных проекта. Позиции без цены названы «по КП» (172 шт.) и в итог не входят: пока цена не названа, итог выше напечатанного.
2. Вилка: «от» — сумма по позициям с ценой по нижней границе открытых прайсов (прайсы собраны 21.09.2026, часть расценок сверена повторно 08.11.2026, Москва); «до» — «от» плюс резерв на непредвиденное (15 % от ремонта; частный ремонт 10–20 %).
3. Работы — ориентир по прайсам подрядчиков, не договорная цена: расценку называет бригада после контрольного обмера. Материалы — по «Смете материалов с ценами» (следующий лист).
4. Разбивка по помещениям — доли: общая закупка делится пропорционально площади (длине, числу), по которой считается позиция; работы — по объёму строки в помещении. Сумма по помещениям, по этапам и по категориям одна и та же.
5. Источники расценок и цен: Ц1 — Домашний мастерок: прайс на отделочные работы, 2026; Ц2 — Домашний мастерок: прайс на плиточные работы, 2026; Ц3 — Домашний мастерок: прайс на электромонтажные работы, 2026; Ц4 — Профи ремонтник: штукатурно-малярные работы; Ц5 — Profi.ru: укладка керамогранита на стены, Москва 2026; Ц6 — справочник материалов: ориентир по сегментам; Ц7 — Розница Москвы, 09.2026: Лемана ПРО, KGSnab, официальный дилер Farrow & Ball.
6. Оборудование «по КП» из сметы сметчика (кухня и др.): 1 поз. — в позиции «по КП» мебели и техники.

	Лист	№ док.	Подпись	Дата	Проект: Квартира 58 м²			
Дизайнер	Кырлан А.С.			14.11.26				
Проверил					Смета проекта: этапы, помещения, итог (окончание)	Стадия	Лист	Листов
Н. контр.								
Утв.						П	С7	92

выпуск 14.11.2026 № 2b6bd7c078 · стр. 82 из 92

Смета материалов с ценами

№	Позиция	Ед.	Нетто	Запас	С запасом	К закупке (упаковка)	Цена за ед., ₽	Сумма, ₽	Заказать заранее	Доп.
Чистовая отделка — позиций 14, с ценой 10, итого 562 698 ₽										
Покрытия полов и облицовка										
1	Инженерная доска (дуб натуральный, рабочий слой 4 мм, эмиссия E1, прямая укладка)	м²	41,08	7 %	43,96	44,00 м²	4 513 / м²	198 572		1, 8
2	Керамогранит 600×600 мм SG651622R	шт	48	13 %	54	54 шт · коробка	1 800 / м²	34 992		8
3	Керамогранит 1200×600 мм 610015000370	шт	87	13 %	98	98 шт · коробка	3 500 / м²	246 960		8
Лакокрасочные материалы										
4	Краска интерьерная акриловая, полуматовая, класс истирания 1 — Tikkurila S 1002-Y50R	л	9,90	10 %	10,89	5 банка · банка 2,7 л	3 510 / банк	17 550		8
5	Краска интерьерная водно-дисперсионная, глубокоматовая, класс истирания 1 — Tikkurila S 0300-N	л	11,83	10 %	13,01	5 банка · банка 2,7 л	3 510 / банк	17 550		8
6	Краска интерьерная акриловая, глубокоматовая, класс истирания 2 — Tikkurila S 1502-Y50R	л	8,14	10 %	8,95	4 банка · банка 2,7 л	3 510 / банк	14 040		8
7	Краска интерьерная акриловая, полуматовая, класс истирания 1 — Tikkurila S 1502-Y50R	л	5,44	10 %	5,98	3 банка · банка 2,7 л	3 510 / банк	10 530		8
8	Краска интерьерная акриловая, матовая, класс истирания 1 — Tikkurila Harmony V503 «Winter»	л	5,92	10 %	6,51	3 банка · банка 2,7 л	3 510 / банк	10 530		8
9	Краска интерьерная акриловая, глубокоматовая, класс истирания 2 — Tikkurila Anti-Reflex 2 V503 «Winter»	л	1,43	10 %	1,57	1 банка · банка 2,7 л	3 510 / банк	3 510		8
Погонажные изделия и потолки										
10	Плинтус напольный МДФ под покраску, h=110 мм, крепление к стене — SX184	м	48,82	10 %	53,70	23 шт · хлыст 2,4 м	368 / шт	8 464		8
Двери										
11	Дверь входная Д-1, проём 900×2100 мм	шт	1		1	1 шт	по запросу			6
12	Дверь скрытого монтажа (короб под покраску) Д-2, проём 900×2100 мм, Софья (SOFIA) Скрытые двери Модель 07	шт	1		1	1 шт	по запросу		≈ 30 дн.	6, 7
13	Дверь скрытого монтажа (короб под покраску) Д-3, проём 800×2100 мм, Софья (SOFIA) Скрытые двери Модель 07	шт	2		2	2 шт	по запросу		≈ 30 дн.	6, 7
14	Дверь скрытого монтажа (короб под покраску) Д-4, проём 700×2100 мм, Софья (SOFIA) Скрытые двери Модель 07	шт	2		2	2 шт	по запросу		≈ 30 дн.	6, 7
Черновые материалы — позиций 13, с ценой 2, итого 23 400 ₽										
Покрытия полов и облицовка										
15	Клей для паркетной и инженерной доски (эластичный, по ТУ изготовителя доски)	м²	41,08		41,08	фасовка по ТУ изделия	по запросу			2
Сухие смеси и гидроизоляция										
16	Клей плиточный цементный класса C2 S1 (ГОСТ Р 56387-2018)	кг	24,94	10 %	27,43	2 мешок · мешок 25 кг	1 800 / меш.	3 600		8
17	Клей плиточный цементный класса C2 (ГОСТ Р 56387-2018)	кг	240,94	10 %	265,03	11 мешок · мешок 25 кг	1 800 / меш.	19 800		8
18	Затирка цементная класса класс не задан, цвет — по колерной карте	кг	3,51	10 %	3,86	2 упаковка · упак. 2 кг	по запросу			
19	Гидроизоляция обмазочная полимерная, 2 слоя, лента в углах, манжеты на выводах	м²	7,07	10 %	7,78	фасовка по ТУ изделия	по запросу			2
20	Лента демпферная по периметру пола из плитки	м	19,14	10 %	21,05	22,00 м	по запросу			
21	Смесь цементно-песчаная для стяжки M200 (50 мм, 33 мм)	м³	2,71	5 %	2,85	фасовка по ТУ изделия	по запросу			2
22	Смесь штукатурная гипсовая для машинного и ручного нанесения по маякам, слой до 10 мм	м²	24,67	10 %	27,14	фасовка по ТУ изделия	по запросу			2
Короба из ГКЛВ										

	Лист	№ док.	Подпись	Дата	Проект: Квартира 58 м²			
Дизайнер	Кырлан А.С.			14.11.26	Смета материалов с ценами	Стадия	Лист	Листов
Проверил						П	С8	92
Н. контр.								
Утв.								

выпуск 14.11.2026 № 2b6bd7c078 · стр. 83 из 92

Смета материалов с ценами (продолжение)

№	Позиция	Ед.	Нетто	Запас	С запасом	К закупке (упаковка)	Цена за ед., ₽	Сумма, ₽	Заказать заранее	Доп.
23	Лист ГКЛВ 12,5 мм, 2500 × 1200 мм, обшивка коробов в 2 слоя	м²	4,22	10 %	4,64	2 лист · лист 3,00 м²	по запросу			
24	Профиль стальной оцинкованный 27 × 28 мм: каркас коробов (стойки и направляющие)	м	12,08	10 %	13,29	5 шт · хлыст 3 м	по запросу			
Лакокрасочные материалы										
25	Шпаклёвка финишная полимерная под окраску (стены и потолки, Q3)	м²	177,72	10 %	195,49	фасовка по ТУ изделия	по запросу			2
26	Грунтовка акриловая глубокого проникновения, 2 слоя	м²	208,78	10 %	229,66	фасовка по ТУ изделия	по запросу			2
Погонажные изделия и потолки										
27	Потолок подвесной ГКЛ/ГКЛВ по каркасу Knauf П113: листы, профили, подвесы, лента, шпаклёвка швов	м²	49,29		49,29	фасовка по ТУ изделия	по запросу			2
Электрика и слаботочные сети — позиций 31, с ценой 0, итого 0 ₽										
Слаботочные сети										
28	Кабель домофона — тип по системе поставщика	м	3,40		3,40	4,00 м	по запросу			3
29	Кабель коаксиальный RG-6 (75 Ом) к розеткам ТВ	м	16,30		16,30	17,00 м	по запросу			3
30	Кабель U/UTP кат. 5e (LAN, Wi-Fi и камеры по PoE)	м	30,10		30,10	31,00 м	по запросу			3
31	Гофротруба Ø20 для слаботочных линий, отдельно от силовых	м	44,80		44,80	45,00 м	по запросу			3
32	Розетка компьютерная RJ45, кат. 6, с рамкой и подрозетником	шт	2		2	2 шт	по запросу			
33	Розетка телевизионная (коаксиальная) с рамкой и подрозетником	шт	1		1	1 шт	по запросу			
34	Трубка или монитор домофона (поставка домофонной организации)	шт	1		1	1 шт	по запросу			
35	Щит слаботочный ЩС: корпус, DIN-рейка, розетки 220 В	шт	1		1	1 шт	по запросу			
36	Патч-панель, портов не менее 2	шт	1		1	1 шт	по запросу			
Электрика: щит										
37	Автоматический выключатель C10 A, 1P	шт	1		1	1 шт	по запросу			4
38	Автоматический выключатель C16 A, 1P	шт	4		4	4 шт	по запросу			4
39	Автоматический выключатель C32 A, 1P	шт	1		1	1 шт	по запросу			4
40	Корпус щита ЩРВ-П-24, IP41, 24 модулей	шт	1		1	1 шт	по запросу			4
41	Вводной автомат C63, 2P	шт	1		1	1 шт	по запросу			4
42	Вводное УЗО-S 63 A, 100 мА (селективное)	шт	1		1	1 шт	по запросу			4
43	УЗИП тип 2	шт	1		1	1 шт	по запросу			4
Электрика: механизмы и изделия										
44	Розетка с з/к и защитными шторками, 16 А	шт	17		17	17 шт	по запросу			4
45	Розетка IP44 с крышкой, 16 А	шт	2		2	2 шт	по запросу			4
46	Выключатель 1-клав.	шт	5		5	5 шт	по запросу			4
47	Выключатель 1-клав. проходной	шт	2		2	2 шт	по запросу			4

	Лист	№ док.	Подпись	Дата	Проект: Квартира 58 м²			
Дизайнер	Кырлан А.С.			14.11.26	Смета материалов с ценами (продолжение)	Стадия	Лист	Листов
Проверил						П	С9	92
Н. контр.								
Утв.								

выпуск 14.11.2026 № 2b6bd7c078 · стр. 84 из 92

Смета материалов с ценами (продолжение)

№	Позиция	Ед.	Нетто	Запас	С запасом	К закупке (упаковка)	Цена за ед., ₽	Сумма, ₽	Заказать заранее	Доп.
48	Выключатель 2-клав. проходной	шт	2		2	2 шт	по запросу			4
49	Рамка 1-постовая	шт	24		24	24 шт	по запросу			4
50	Рамка 2-постовая	шт	2		2	2 шт	по запросу			4
51	Коробка установочная (подрозетник) Ø68	шт	28		28	28 шт	по запросу			4
52	Вывод кабеля под прибор (клеммник)	шт	3		3	3 шт	по запросу			4
53	Вывод кабеля к вентилятору вытяжки	шт	1		1	1 шт	по запросу			4
54	Коробка уравнивания потенциалов КУП	шт	1		1	1 шт	по запросу			4
55	Блок питания LED 24 В, 100 Вт	шт	1		1	1 шт	по запросу			4
56	Блок питания LED 24 В, 60 Вт	шт	1		1	1 шт	по запросу			4
57	Извещатель дымовой автономный	шт	2		2	2 шт	по запросу			4
58	Извещатель тепловой	шт	1		1	1 шт	по запросу			4
Сантехника — позиций 34, с ценой 0, итого 0 ₽										
Сантехника: санитарные приборы										
59	Ванна встраиваемая акриловая 1500×700 мм, с каркасом, экраном и отверстием слив-перелив — акриловая 1500×700, смеситель настенный	шт	1		1	1 шт	по запросу			5
60	Унитаз подвесной безободковый, с сиденьем микролифт, крепёж и звукоизолирующая прокладка — Laufen Pro 8.2096.6.000.000.1	шт	1		1	1 шт	по запросу			5
61	Инсталляция для подвесного унитаза: рама высотой 1120 мм, бачок, клавиша смыва (ось клавиши 1050 мм от чистого пола)	шт	1		1	1 шт	по запросу			5, 1
62	Умывальник подвесной 450×450 мм, с отверстием под смеситель и переливом — Laufen Pro S 8.1096.3.000.104.1	шт	1		1	1 шт	по запросу			5
63	Мойка кухонная 700×480 мм, с переливом — мойка врезная 700×480 в шкафу М-02	шт	1		1	1 шт	по запросу			5
64	Полотенцесушитель электрический, IP44, с терморегулятором	шт	1		1	1 шт	по запросу			5, 1
Сантехника: смесители, сифоны и арматура приборов										
65	Смеситель для ванны настенный однорычажный, межосевое 150 мм, с душевым набором (лейка, шланг, держатель)	шт	1		1	1 шт	по запросу			5, 1
66	Смеситель для умывальника однорычажный, с донным клапаном	шт	1		1	1 шт	по запросу			5, 1
67	Смеситель кухонный однорычажный, высокий излив	шт	1		1	1 шт	по запросу			5, 1
68	Обвязка ванны слив-перелив Ø40/50 с сифоном	шт	1		1	1 шт	по запросу			5, 1
69	Сифон для умывальника бутылочный Ø32/40–50, с гофрой к выпуску	шт	1		1	1 шт	по запросу			5, 1
70	Сифон для мойки Ø40/50	шт	1		1	1 шт	по запросу			5, 1
71	Сифон для стиральной машины встраиваемый в стену Ø50, с обратным клапаном	шт	1		1	1 шт	по запросу			5, 1
72	Кран угловой ½"×½" с гибкой подводкой 40 см (умывальники, мойка)	шт	4		4	4 шт	по запросу			5, 1
73	Кран шаровой угловой ½"×¾" для подключения стиральной и посудомоечной машины	шт	1		1	1 шт	по запросу			5, 1
Сантехника: трубопроводы										
74	Труба полипропиленовая PP-R PN20 Ø20×3,4 (B1) — ГОСТ 32415-2013	м	13,50	10 %	13,50	13,50 м	по запросу			5

	Лист	№ док.	Подпись	Дата	Проект: Квартира 58 м²			
Дизайнер	Кырлан А.С.			14.11.26	Смета материалов с ценами (продолжение)	Стадия	Лист	Листов
Проверил						П	С10	92
Н. контр.								
Утв.								

выпуск 14.11.2026 № 2b6bd7c078 · стр. 85 из 92

Смета материалов с ценами (продолжение)

№	Позиция	Ед.	Нетто	Запас	С запасом	К закупке (упаковка)	Цена за ед., ₽	Сумма, ₽	Заказать заранее	Доп.
75	Труба PP-R, армированная стекловолокном, PN20 Ø20×2,8 (Т3) — ГОСТ 32415-2013	м	9,50	10 %	9,50	9,50 м	по запросу			5
76	Труба канализационная ПП Ø40 (К1) — ГОСТ 32414-2013	м	2,50	10 %	2,50	2,50 м	по запросу			5
77	Труба канализационная ПП Ø50 (К1) — ГОСТ 32414-2013	м	8,00	10 %	8,00	8,00 м	по запросу			5
78	Труба канализационная ПП Ø110 (К1) — ГОСТ 32414-2013	м	1,50	10 %	1,50	1,50 м	по запросу			5
Сантехника: фасонные части и выводы										
79	Отвод канализационный ПП 45° Ø40 — ГОСТ 32414-2013	шт	2		2	2 шт	по запросу			5
80	Отвод канализационный ПП 45° Ø50 — ГОСТ 32414-2013	шт	12		12	12 шт	по запросу			5
81	Отвод канализационный ПП 45° Ø110 — ГОСТ 32414-2013	шт	6		6	6 шт	по запросу			5
82	Тройник канализационный ПП 45° (врезки ветвей) — ГОСТ 32414-2013	шт	4		4	4 шт	по запросу			5
83	Ревизия канализационная ПП (после поворота трассы) — ГОСТ 32414-2013	шт	5		5	5 шт	по запросу			5
84	Фитинги PP-R Ø20: тройники, угольники 90° (ветви и повороты В1, Т3) — ГОСТ 32415-2013	шт	22		22	22 шт	по запросу			5
85	Водорозетка PP-R Ø20×½" настенная, с креплением — ГОСТ 32415-2013	шт	8		8	8 шт	по запросу			5
Сантехника: узлы ввода, люки, короба										
86	Кран шаровой латунный Ду15 PN16 (отключение ввода)	шт	2		2	2 шт	по запросу			5, 1
87	Фильтр сетчатый косой Ду15	шт	2		2	2 шт	по запросу			5, 1
88	Счётчик воды крыльчатый Ду15 (ХВ, ГВ), с поверкой	шт	2		2	2 шт	по запросу			5, 1
89	Клапан обратный Ду15	шт	2		2	2 шт	по запросу			5, 1
90	Люк ревизионный нажимной под плитку 300×400 мм	шт	1		1	1 шт	по запросу			5, 1
91	Звукоизоляция стояка К1 в коробе: рулонный звукоизоляционный материал ≥ 10 мм, обмотка стояка на высоту этажа	м	2,70		2,70	2,70 м	по запросу			5, 1
92	Короб К1 над полом: профиль ПН/ПС, ГКЛВ 12,5 мм под плитку	м	1,60		1,60	1,60 м	по запросу			5, 1
	ИТОГО материалы (позиций с ценой 12 из 92; без цены 80 — «по запросу», в итог не входят)							**586 098**		

Примечания


1. Количества — из единой книги материалов проекта: тот же расход, что в спецификации отделочных материалов, смете и списке покупок. Запас — на подрезку и бой; норма запаса печатается в графе «Запас», её основание — в отдельном документе «Смета на материалы».
2. Цены — нижняя граница открытых прайсов (прайсы собраны 21.09.2026, часть расценок сверена повторно 08.11.2026, Москва); не предложение (оферта) магазинов. Цены нет — «по запросу», позиция в итог не входит. Работы в эту смету не входят (они — на листе «Смета проекта»).
3. Доп. 1. Изделие не выбрано: позиция описана по характеристикам («аналог»); марка, артикул и цена определяются при выборе изделия.
4. Доп. 2. Фасовка не задана в данных: количество дано в мерах расчёта, число упаковок определяется по выбранному продукту (расход и тара — по ТУ).
5. Доп. 3. Длина кабеля — по длинам групп щита из данных электрика; запас на подрезку в длину не заложен — берите бухту с запасом 5–10 %.
6. Доп. 4. Механизмы, рамки и подрозетники — по ведомости изделий электрика; серию механизмов выбирает заказчик.
7. Доп. 5. Трубы и фасонные части — по трассам листа разводки, +10 % на подрезку (уже в количестве); модели приборов заказчик выбирает сам.
8. Доп. 6. Двери: цена и срок называет поставщик после выбора изделия; в смету стоят только если цена задана в данных.
9. Доп. 7. Срок поставки — из данных проекта; если срок не задан, указан типовой диапазон практики как ориентир, а не срок поставщика.
10. Доп. 8. Цена — нижняя граница открытых прайс-листов на дату сбора (книга цен проекта); не коммерческое предложение магазина.
11. Доп. 9. Доли по помещениям справочные: общая закупка делится пропорционально площади (длине, числу), по которой считается позиция.

	Лист	№ док.	Подпись	Дата	Проект: Квартира 58 м²			
Дизайнер	Кырлан А.С.			14.11.26	Смета материалов с ценами (окончание)	Стадия	Лист	Листов
Проверил						П	С11	92
Н. контр.								
Утв.								

выпуск 14.11.2026 № 2b6bd7c078 · стр. 86 из 92

1 Порог 15 мм: мокрая зона — смежное помещение (М 1:5)


Применение: двери Д-4

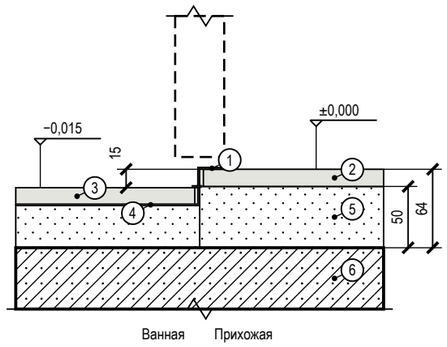

Поз.	Состав слоя, изделие
1	порог-переход металлический, перепад 15 мм, на клей-герметик
2	керамогранит на клею C2 TE S1
3	керамогранит на клею C2 TE S1
4	гидроизоляция в 2 слоя с подъёмом на торец ступени, лента в углу
5	ЦПС М200 50 мм; в мокрой зоне 33 мм
6	плита перекрытия

2 Дверь скрытого монтажа в плоскости стены, плинтус (М 1:5)


Применение: двери Д-2, Д-3, Д-4

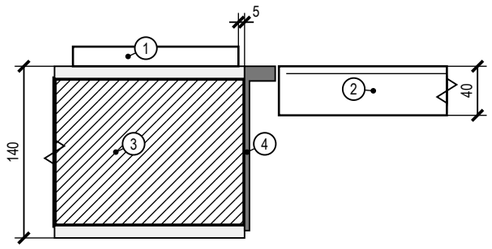

Поз.	Состав слоя, изделие
1	плинтус МДФ 110×16 на клей; у короба — зазор 5 мм, окраска в цвет стены
2	полотно 40 мм под окраску, заподлицо со стеной; теневой шов 3 мм
3	стена 120 мм, штукатурка 10 мм с двух сторон
4	короб скрытого монтажа (алюминий), лицом в плоскости отделки; монтаж до штукатурки

3 Короб стояков К1-1 с люком и звукоизоляцией (М 1:10)


Применение: пом. 3

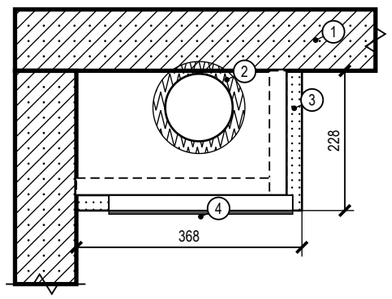

Поз.	Состав слоя, изделие
1	стены существующие — не ослаблять
2	звукоизоляция стояков рулонная 20 мм; К1-1 Ø110
3	короб: профиль 27×28, ГКЛВ 2×12,5 мм, облицовка плиткой
4	ревизионный люк 300×400 мм нажимной, под плитку; против ревизии стояка

4 Гидроизоляция санузла: заход на стены 200 мм, примыкание ванны (М 1:20)


Применение: пом. 3, 4

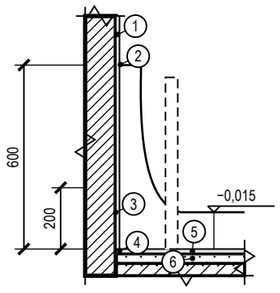

Поз.	Состав слоя, изделие
1	облицовка — плитка на клею C2 TE S1, затирка CG2WA
2	примыкание ванны: лента бордюрная + силиконовый санитарный герметик; облицовка опирается на борт
3	гидроизоляция обмазочная в 2 слоя, заход на стены 200 мм (в зоне душа — выше), до облицовки; акт скрытых работ, тест проливом
4	лента гидроизоляционная в углах и у трапов
5	керамогранит на клею C2 TE S1
6	ЦПС М200 33 мм

5 Плинтус МДФ 110×16 мм у окрашенной стены по доске (ламинату) (М 1:10)


Применение: пом. 1, 2, 6

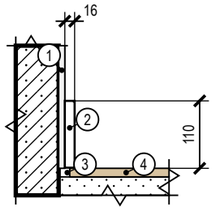

Поз.	Состав слоя, изделие
1	штукатурка, шпаклёвка Q3, окраска — по ведомости отделки
2	плинтус МДФ 110×16 под окраску в цвет стены; клей монтажный — к стене, не к полу
3	зазор покрытия у стены 8–10 мм закрывается плинтусом
4	инженерная доска на клею

6 Плинтус МДФ 110×16 мм у окрашенной стены по керамограниту (плитке) (М 1:10)

Применение: пом. 5

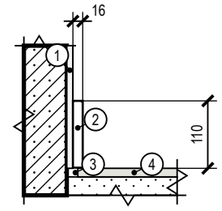

Поз.	Состав слоя, изделие
1	штукатурка, шпаклёвка Q3, окраска — по ведомости отделки
2	плинтус МДФ 110×16 под окраску в цвет стены; клей монтажный — к стене, не к полу
3	зазор покрытия у стены 8–10 мм закрывается плинтусом
4	керамогранит на клею C2 TE S1

Условные обозначения

- железобетон (плита, стены) — условно: конструкция не установлена
- кладка, перегородка — условно: конструкция не установлена
- стяжка, раствор
- гипсокартон ГКЛВ
- звукоизоляция, эластичный заполнитель
- плитка, керамогранит на клею
- инженерная доска (покрытие пола)
- металлический профиль (порог, Т-профиль, короб двери)
- гидроизоляция (обмазочная, лента)

Примечания

1. Узлы — типовые решения проекта для мест, отмеченных выносками на листе схемы расположения развёрток и узлов; размеры — в мм, отметки — в м от ±0,000.
2. Узлы с гидроизоляцией, закладными и коробами скрытого монтажа принимаются по актам скрытых работ до закрытия отделкой; гидроизоляция — после теста проливом (24 ч).
3. Марки изделий (порог, Т-профиль, короб скрытой двери, люк) — по спецификациям; замена — на аналог с теми же габаритами по согласованию с автором проекта.
4. Материал плиты перекрытия и стен в узлах показан условно (железобетон, кладка): конструкция дома не установлена — крепёж, анкеры и толщины слоёв уточняются после обследования (до него — по допущениям общих указаний).


	Лист	№ док.	Подпись	Дата
Дизайнер	Кырлан А.С.			14.11.26
Проверил				
Н. контр.				
Утв.				

Проект: Квартира 58 м²

Узлы	Стадия	Лист	Листов
	П	С12	92

выпуск 14.11.2026 № 2b6bd7c078 · стр. 87 из 92

№	Работа	Нед.	После
Р-1	**демонтаж**	1	
Р-2	**контрольный обмер**	0,5	Р-1
Р-3	**черновая электрика**	1,25	Р-2
Р-4	черновая сантехника	1	Р-2
Р-5	**штукатурка**	2	Р-3, Р-4
Р-6	**стяжка**	0,75	Р-5
Р-7	**гидроизоляция**	0,5	Р-6
Р-8	ГКЛ	1,25	Р-3, Р-4
Р-9	**плитка**	2,5	Р-7, Р-8, Р-6
Р-10	**шпаклёвка**	2,25	Р-9, Р-8, Р-5
Р-11	**окраска**	1,75	Р-10
Р-12	**чистовые полы**	1	Р-11, Р-9
Р-13	**двери и плинтусы**	0,75	Р-12, Р-11
Р-14	**чистовая электрика и сантехника**	0,75	Р-13, Р-11
Р-15	**кухня и мебель**	0,75	Р-14, Р-13
Р-16	**сдача**	0,5	Р-15, Р-14
Закупки: заказать не позднее — «◆»; от заказа до поставки — штриховая полоса; срок поставки — только из данных или «ориентир практики»			
З-1	Двери скрытого монтажа с коробом под покраску в существующих проёмах: Д-2, Д-3, Д-4 — 5 шт	4,25	для Р-5
З-2	Кухонный гарнитур по проекту кухни: модули М-01, М-02, М-03, М-04, М-05, М-06, М-07	6	для Р-15
З-3	Встраиваемая техника кухни: М-01 холодильник, М-05 стиральная машина		для Р-15
З-4	Стиральная машина: ОБ-02 (вертикальная загрузка 400 × 600 мм — условие закупки)		для Р-4
З-5	Сантехнические приборы и инсталляции: С-01, С-02, С-03, С-05		для Р-4
З-6	Керамогранит и плитка: 2 поз. по артикулу и формату, 46,11 м² по раскладке		для Р-9
З-7	Покрытие пола (доска) и плинтус: пом. 1, 2, 6		для Р-12
З-8	Встроенная мебель по замеру цеха: М-15	6	для Р-15

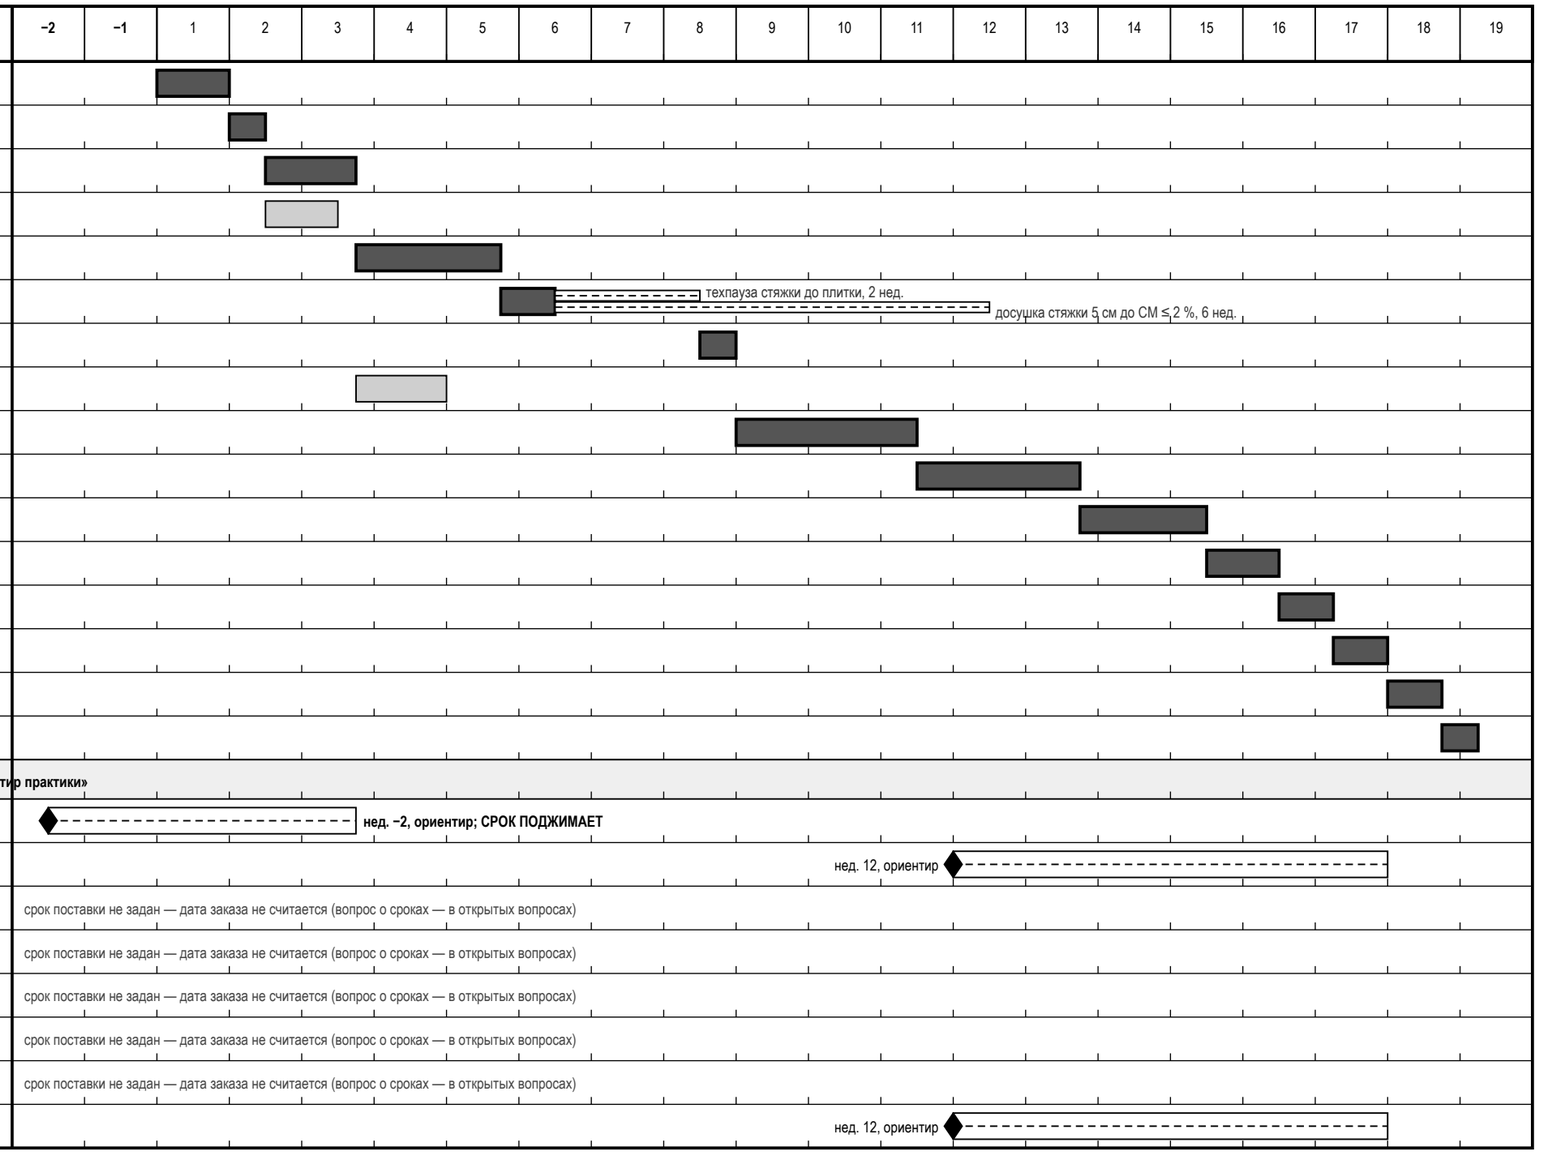

Итого: ≈ 18,25 нед. · жирная линия и тёмная полоса — критический путь

Примечания

1. Длительности этапов — типовые сроки по площади 55,23 м² (таблица «Свод для графика»: недели по этапам для 45, 80 и 120 м², середина вилки, линейная интерполяция); это ориентир, а не норма и не обещание бригады. Контрольный обмер — ориентир 0,5 нед. (в таблице нет).
2. Зависимости «после» — из графика закупок и работ (лист «График закупок и работ»); каждая работа начинается после конца предшественников. Техпаузы стоят отдельными полосами, а не спрятаны в длительности: стяжка → плитка — не менее 2 нед.; стяжка → чистовой пол — досушка стяжки 5 см до СМ ≤ 2 % — 6 нед. (ориентир «1 нед. на 1 см до 4 см, 5 см — 6 нед., 6 см — 8 нед.»; решает замер).
3. График последовательный и поэтому консервативный: в жизни шпаклёвка, плитка и досушка стяжки идут частично параллельно (таблица типовых сроков для 55,23 м²: 13–16 нед.). Совмещения — решение прораба после обмера.
4. Закупки: «заказать не позднее» = начало работы, которой нужна позиция, минус срок поставки. Срок поставки — из данных проекта (срок поставки позиции, срок изготовления обоев в отделке); если его нет, в графике стоит типовой диапазон практики с пометкой «ориентир» — это не срок поставщика, его надо получить до заказа. Кухню и встроенную мебель заказывают после замера по готовым стенам (после штукатурки). Позиции без срока дат заказа не имеют.
5. «Срок поджимает»: самая поздняя дата заказа раньше, чем позицию можно заказать (до замера или обмера): сдвиньте начало работ, ищите изделие с меньшим сроком или заказывайте по предварительному размеру — решение прораба и заказчика.

	Лист	№ док.	Подпись	Дата	Проект: Квартира 58 м²			
Дизайнер	Кырлан А.С.			14.11.26	Календарный график работ и закупок	Стадия	Лист	Листов
Проверил						П	С13	92
Н. контр.								
Утв.								

выпуск 14.11.2026 № 2b6bd7c078 · стр. 88 из 92

Приёмка по этапам: контрольные точки, допуски и акты скрытых работ

Этап	Контрольная точка (дальше не пускают без подписи)	Что проверяют	Чем	Допуск	Основание	Подпись	Акт скрытых работ / документ
Р-1	Демонтаж До начала демонтажа: запрошены документы на дом и БТИ	Что снимается и что не трогается: покрытия, отделка, дверные блоки; несущие стены и перегородки — без изменений	осмотр по плану демонтажа	снятое — только по плану; несущее не затрагивать	практика		Фото помещений до и после демонтажа; перечень снятого в журнале работ.
Р-2	Контрольный обмер Контрольный обмер на голых стенах сделан до заказа всего, что делают по размеру	Размеры помещений и проёмов, диагонали, положение стояков, щитка, каналов, толщины стен	рулетка, лазерный дальномер, уровень	допуск задаёт проект; расхождение с планом — в перечень открытых вопросов до заказа	практика		Протокол контрольного обмера с эскизом; расхождения занесены в открытые вопросы.
Р-3	Черновая электрика Черновая электрика: трассы, высоты подрозетников, замер изоляции подписаны до заделки	Сопротивление изоляции проводки (цепи до 1000 В)	мегаомметр	не менее 0,5 МОм	норматив (ПУЭ, гл. 1.8)		Акт скрытых работ на трассы проводки и слаботочные линии до закрытия штукатуркой и ГКЛ; исполнительная схема трасс с привязками; заземление и уравнивание потенциалов в санузле протокол и фото.
		Целостность и маркировка: PE жёлто-зелёный, N — синий, L — прочие цвета	визуально, прозвонка	каждый проводник промаркирован	практика		
		Высоты подрозетников и привязки — по плану розеток и выключателей	рулетка, уровень	по проекту; от чистого пола	практика		
Р-4	Черновая сантехника Черновая сантехника: опрессовка, отметки выводов, инсталляции подписаны до зашивки	Опрессовка водоснабжения: рабочее давление до 0,6 МПа — испытание 0,9 МПа; выше 0,6 МПа — по расчёту	опрессовочный насос, манометр	выдержка 10 мин (поквартирная); падение: пластик не более 0,06 МПа за 30 мин, сталь не более 0,05 МПа за 10 мин	практика (СП 73.13330)		Акт опрессовки (давление, время, результат); акт скрытых работ на трассы в стенах, полу и коробах; инсталляции, скрытые смесители, трапы — фото с рулеткой и отметками.
		Уклон канализации Ø40–50	уровень, построитель плоскостей	не менее 20 мм на 1 м	норматив (СП 30.13330)		
		Протечки в соединениях, сифоны, смесители, гибкая подводка	осмотр под давлением, салфетка на стыках	нет капель и влажных следов в контрольное время	практика		
		Отметки выводов и положение инсталляций до зашивки и гидроизоляции	рулетка в кадре, фото	по листу выводов	практика		
Р-5	Штукатурка Маяки стен проверены до штукатурки; коробки скрытых дверей стоят до штукатурки	Отклонение от вертикали (простая / улучшенная / высококачественная штукатурка)	отвес, лазерный уровень	3 / 2 / 1 мм на 1 м; не более 15 / 10 / 5 мм на высоту	практика (СП 71.13330.2017)		Фото коробок скрытых дверей с отметкой чистого пола — до штукатурки; класс штукатурки (простая / улучшенная / высококачественная) назван в договоре.
		Отклонение от горизонтали	уровень, правило	3 / 2 / 1 мм на 1 м; не более 15 / 10 / 5 мм на длину	практика (СП 71.13330.2017)		
		Неровности (плоскостность)	правило 2 м и щуп	до 5 / 3 / 2 мм на 1 м; не более 3 / 2 / 2 неровностей на 4 м²	практика (СП 71.13330.2017)		
		Влажность основания перед шпаклёвкой и отделкой	влагомер	верхние 20–30 мм — не более 5 % по массе	норматив (СП 71, табл. 7.2)		
Р-6	Стяжка Стяжка: подготовка, после заливки ровность, затем замер СМ перед чистовым полом	Ровность: просвет под рейкой 2 м	рейка 2 м, клиновой щуп	под паркет, ламинат — 2 мм; под гидроизоляцию до 4 мм; прочие покрытия — до 6 мм (цифры расходятся между источниками — сверить перед актом)	практика (СП 29.13330)		Акт скрытых работ на стяжку (толщина, армирование) до чистового пола; протокол ровности и протокол СМ-влажности; звукоизоляция и демпферная лента под стяжкой — фото и паспорт; контуры тёплого пола до заливки — схема укладки и замер сопротивления.
		Отклонение от горизонтали по помещению	уровень, нивелир	не более 0,2 % длины помещения	практика (СП 29.13330)		

	Лист	№ док.	Подпись	Дата
Дизайнер	Кырлан А.С.			14.11.26
Проверил				
Н. контр.				
Утв.				

Проект: Квартира 58 м²

Чек-лист приёмки по этапам. Лист 1 из 3

Стадия	Лист	Листов
П	С14	92

выпуск 14.11.2026 № 2b6bd7c078 · стр. 89 из 92

Приёмка по этапам: контрольные точки, допуски и акты скрытых работ (продолжение)

Этап	Контрольная точка (дальше не пускают без подписи)	Что проверяют	Чем	Допуск	Основание	Подпись	Акт скрытых работ / документ
		Число точек измерения	рейка	не менее 3 на 30 м² или 1 на небольшое помещение	практика		
		Отслоения и пустоты	простукивание молотком или киянкой	глухой звук — зона вскрывается и переделывается	практика		
		Влажность перед укладкой доски: цементная стяжка	влагомер; СМ-замер	ЦПС не более 2,0 % СМ (с тёплым полом не более 1,8 %); влагомер для плитки — не более 5 %	практика (СП 71; рекомендации производителей)		
Р-7	Гидроизоляция Гидроизоляция: пролив 24 ч подпись до плитки	Заведение на стены не ниже 200 мм от чистого пола; за ванной — 300 мм выше борта; в душе без поддона — на высоту лейки	рулетка	не менее 200 мм	норматив (СП 71.13330.2017, п. 8.6.5); остальное — практика		Акт теста проливом, фото узлов и высоты заведения на стены — до плитки.
		Тест проливом: слой воды 10–30 мм, контроль уровня и потолка соседа снизу	линейка, визуально	24 ч (минимум 12 ч); падения уровня и протечки нет	практика		
		Два слоя обмазки с межслойной сушкой, лента в углах и манжеты на выводах	визуально	по инструкции производителя	практика		
Р-8	ГКЛ Короба, ниши и потолки: черновые сети в зоне коробов приняты до обшивки	Шаг саморезов, отступ от кромки, заделка стыков (как у перегородок)	рулетка, визуально	потолок 150 мм; кромка 5–10 мм; стык — лента и 2 слоя шпаклёвки	практика (СП 163.1325800.2014)		Акт скрытых работ: каркас ГКЛ, закладные, звукоизоляция — фото до обшивки; воздуховоды в коробах и за потолком — фото и схема.
		Закладные под тяжёлое, карнизы, подвесные светильники на месте до обшивки	фото с привязками	по плану потолков и узлам	практика		
		Ревизионные люки: доступ к арматуре и ревизиям сохранён	осмотр	по листу ВК	практика		
Р-9	Плитка Раскладка плитки: первая плита и первый ряд проверены по развёртке; плитка выбрана, калибр партии измерен	Уступы между смежными плитками	линейка, на просвет	не более 1 мм	норматив (СП 71.13330.2017)		Раскладка подписана до начала плитки; протокол первого ряда; акт теста проливом приложен (этап гидроизоляции).
		Ширина шва и его прямолинейность	линейка, калибр	до 6 мм ручная укладка; фактическая по проекту ±0,5 мм	практика		
		Отклонение рядов от вертикали и горизонтали	уровень, правило, отвес	1,5 мм на 1 м длины	практика		
		Ровность облицовки	правило 2 м и щуп	не более 2–4 мм (цифра расходится по источникам)	практика		
		Пустоты под плиткой	простукивание всей площади	до 10 % площади допустимо; свыше 25 % под одной плиткой — брак	практика		
Р-10	Шпаклёвка Шпаклёвка Q3/Q4: проверка боковым светом до окраски	Класс основания под окраску: Q3 — сплошное финишное шпаклевание; Q4 — под направленный свет	переносной прожектор у поверхности под острым углом	Q3: царапины от абразива до 0,5 мм; Q4 — без видимых царапин и теней; неровность на 2 м: Q3 — 1 мм, Q4 — 0,5 мм	практика (Q-классы — не норматив СП, а согласованный критерий)		Класс (Q3 или Q4) назван в договоре; грунтование и армирование стыков перед шпаклёвкой — запись в журнале.
Р-11	Окраска Выкрасы утверждены, колеровка одной партией	Окраска без полос, подтёков, пропусков; цвет — по колерной карте	боковой свет, образец выкраса	без видимых дефектов при боковом свете	практика		Утверждённые выкрасы; остаток колеровки одной партии — для подкраски.
		Основание сухое, огрунтованное; защита от прямого солнца при высыхании	осмотр	по ТУ краски	норматив (СП 71.13330.2017, п. 7.5.2)		

	Лист	№ док.	Подпись	Дата
Дизайнер	Кырлан А.С.			14.11.26
Проверил				
Н. контр.				
Утв.				

Проект: Квартира 58 м²

Чек-лист приёмки по этапам. Лист 2 из 3

Стадия	Лист	Листов
П	С15	92

выпуск 14.11.2026 № 2b6bd7c078 · стр. 90 из 92

Приёмка по этапам: контрольные точки, допуски и акты скрытых работ (продолжение)

Этап	Контрольная точка (дальше не пускают без подписи)	Что проверяют	Чем	Допуск	Основание	Подпись	Акт скрытых работ / документ
Р-12	Чистовые полы Чистовые полы: влажность, ровность, уступы, зазоры — до укладки доски; мокрые работы закончены	Деформационный зазор у стен и порогов (доска, ламинат)	линейка, клинья при укладке	8–15 мм (чаще 10 мм); у ламината 5–10 мм по СП 71	практика (требования производителей); норматив (СП 71, п. 8.10.14)		Протокол СМ-влажности стяжки до укладки; паспорт и партия доски.
		Перепад основания под покрытие	правило 2 м и щуп	не более 2 мм на 2 м	практика		
		Зазоры и перепады между досками; скрип; видимый зазор в замке — брак	щуп, рука, шаг	«ступеньки» нет	практика		
		Влажность помещения при укладке и после	гигрометр	не более 60 %, без сквозняков	норматив (СП 71, п. 8.1.7)		
Р-13	Двери и плинтусы Полотна и плинтусы — после чистового пола; скрытые полотна после чистовой отделки стен	Отклонение коробки от вертикали	отвес, уровень	1,5 мм на 1 м, не более 3 мм на коробку	практика (ТР 105-00, пересказ)		Коробки скрытых дверей приняты до штукатурки (этап штукатурки); паспорт на полотна.
		Зазор между полотном и коробкой по периметру	щуп	2–4 мм по бокам и верху (единого норматива нет)	практика		
		Открывание и закрывание: без перекоса, плавный ход петель и доводчика	визуально, от руки	без задевания коробки и пола	практика		
Р-14	Чистовая электрика и сантехника Чистовая электрика и сантехника: протокол электролаборатории и проверка УЗО до подписи акта	УЗО: кнопка «Тест»; время отключения; ток отключения	кнопка на аппарате; прибор проверки УЗО (не мультиметр)	отключает; не более 0,3 с; 50–100 % от IΔn	практика измерений		Протокол измерений аккредитованной электролаборатории (изоляция по группам, УЗО, PE, фаза-ноль); исполнительная схема щита; акт опрессовки приложен (этап ВК).
		Сопротивление изоляции готовых линий; петля фаза-ноль для срабатывания автоматов	мегаомметр; прибор петли фаза-ноль	изоляция не менее 0,5 МОм; петля — по проекту	норматив (ПУЭ, гл. 1.8) / по проекту		
		Смесители, сифоны, гибкая подводка: пробный пуск воды	визуально под нагрузкой	нет подтёков в контрольное время	практика		
Р-15	Кухня и мебель Кухня и мебель: замер кухни снят по готовым стенам; чистовая электрика и сантехника подведены	Привязка выводов и розеток к модулям кухни; вытяжка, вентиляция	рулетка, сверка с листом кухни	по проекту кухни	практика		Акт передачи кухни; паспорта техники и гарантийные талоны.
		Тяга вентиляции у решёток	лист бумаги у решётки	бумага притягивается; при сомнениях — замер анемометром	практика		
Р-16	Сдача Финальная приёмка по таблицам СП 71: дефектная ведомость и акт	Стены, потолки, полы, плитка, двери, окна осмотр по чек-листу этапов выше	правило 2 м, уровень, щуп, боковой свет, влагомер	по таблицам выше	практика		Дефектная ведомость и акт приёмки; гарантия: по умолчанию претензии по качеству работ — 2 года, в договоре прописывается отдельно.
		Полный пакет документов: акты скрытых работ, протокол электролаборатории, акт опрессовки, исполнительные схемы, гарантийные обязательства	комплектность	пакет собран до подписи акта	практика		

Примечания

1. Метка основания: «норматив» — цифра подтверждена текстом СП, ГОСТ или ПУЭ; «практика» — отраслевая конвенция или один источник: к спору не годится без сверки первоисточника (СП 71.13330.2017, СП 29.13330, СП 163.1325800.2014, ПУЭ гл. 1.8, СП 73.13330, СП 30.13330).
2. Класс штукатурки (простая / улучшенная / высококачественная) и класс основания под окраску (Q3 или Q4) называются в договоре подряда: допуск выбирается по ним. Q-классы — не норматив, а согласованный сторонами критерий.
3. Акт скрытых работ подписывают до того, как работа закрыта следующим слоем (штукатуркой, плиткой, стяжкой, обшивкой): постфактум он слабее — осматривать нечего. Подписывают заказчик (или технадзор), подрядчик; при перепланировке — автор проекта. Каждую зону снимают до закрытия с рулеткой в кадре и привязкой к стене.
4. По умолчанию, если срок не прописан в договоре, претензии по качеству работ можно предъявить в течение 2 лет со дня приёмки; в договоре гарантийный срок и сроки на скрытые работы рекомендуется назвать явно.

	Лист	№ док.	Подпись	Дата	Проект: Квартира 58 м²			
Дизайнер	Кырлан А.С.			14.11.26	Чек-лист приёмки по этапам. Лист 3 из 3	Стадия	Лист	Листов
Проверил						П	С16	92
Н. контр.								
Утв.								

выпуск 14.11.2026 № 2b6bd7c078 · стр. 91 из 92

Какому мастеру какие листы (номера — как в штампе)

Мастер	Что делает по альбому	Листы	Кроме чертежей — документы	Листов
Замерщик и прораб (до начала работ)	Контрольный обмер на голых стенах, сверка размеров и диагоналей, ответы на открытые вопросы до заказа	12, 14, 71–72	Задание на контрольный обмер; лист открытых вопросов	4
Гипсокартонщик и монтажник перегородок	Демонтаж и возведение перегородок, каркас, короба инсталляции, ниши, потолки; закладные под навесное	15–17, 38–40	Ведомость материалов каркаса; акт скрытых работ на каркас	6
Электрик	Группы щита, подрозетники и высоты, трассы, свет, управление светом, слаботочка, тёплый пол	41–48, 54–70	Таблица нагрузок; ведомость изделий; протокол электролаборатории	25
Сантехник	Выводы воды и канализации, разводка, аксонометрии, инсталляции, короба стояков	25–33, 54–70	Спецификация ВК; акт опрессовки; акт пролива	26
Монтажник вентиляции, отопления и кондиционеров	Вентиляция, радиаторы и тёплые полы, кондиционеры: места, размеры, трассы и дренаж	49–50	Акт опрессовки азотом (кондиционеры); фото воздуховодов до закрытия	2
Штукатур, шпаклёвщик, маляр, паркетчик	Основание стен, окраска и обои по колерной карте, полы и пороги, плинтус, узлы стыков	18–19, 51, 54–70, С1–С2, С12	Колерная карта и выкрасы; спецификация отделочных материалов	23
Плиточник	Раскладка и подрезка плитки стен, пола и фартука, гидроизоляция, швы, выводы в плитке	30–32, 34–35, 52–70, С12	Ведомость плитки; акт теста проливом	25
Монтажник дверей и окон	Заполнение проёмов: размеры коробок, открывание, пороги, скрытые двери	36–37	Ведомость проёмов; паспорта на полотна	2
Мебельщик, кухонный монтажник	Кухня и мебель на заказ: габариты, членение, фурнитура, связка с электрикой и сантехникой	16–17, 20–24, Д1–Д3	Ведомость изделий; замер кухни по готовым стенам	10
Заказчик и комплектатор	Что и когда покупать, сколько с запасом, во что это обойдётся; свет, декор и текстиль; визуализации как должно получиться	1–11, 13, 47, С3–С11, С13	Список покупок; смета; календарный график	23
Прораб и технадзор (приёмка)	Приёмка этапов, акты скрытых работ, дефектная ведомость	С13–С17	Чек-лист приёмки по этапам; календарный график	5

Примечания

1. Номера листов — как в основной надписи: основные подряд (1, 2, 3…), «Д» — детализация мебели, «С» — ведомости, спецификации, узлы и сметы, «П» — приложение единого комплекта. «12–18» — все листы с 12 по 18.
2. Лист может быть у нескольких мастеров: развёртка стены нужна электрику (высоты точек), сантехнику (выводы), отделочнику (материалы) и плиточнику (раскладка). Общие листы (обмер, список листов, перечень вопросов) прораб раздаёт всем.
3. Мастер работает по чертежам и берёт в руки то, что назначено ему здесь; закупки, смету и график ведёт заказчик с прорабом. Лист, которого нет в таблице ни у одного мастера, — вопрос прорабу: чей он.

	Лист	№ док.	Подпись	Дата	Проект: Квартира 58 м²			
Дизайнер	Кырлан А.С.			14.11.26	Лист → мастер	Стадия	Лист	Листов
Проверил						П	С17	92
Н. контр.								
Утв.								

выпуск 14.11.2026 № 2b6bd7c078 · стр. 92 из 92