L

LINEA

ДИЗАЙН-ПРОЕКТ ИНТЕРЬЕРА

Квартира 65 м²

Скандинавский



Визуализация гостиной · 3D

ОБЩАЯ ПЛОЩАДЬ	ПОМЕЩЕНИЙ	СТАДИЯ	ШИФР	ОСНОВА
65,24 м²	9, из них жилых 3	Рабочий проект · предварительно	ГД-2026-007-АИ	план заказчика, без обмера

ПАЛИТРА ОТДЕЛКИ

NCS S 1502-Y50	NCS S 1002-Y50	V503	F&B No. 241	NCS S 0502-Y
31 %	23 %	20 %	12 %	8 %

АВТОР ПРОЕКТА

Кырлан Александр Сергеевич

Ноябрь 2026

Изм.	Кол.уч	Лист	№ док.	Подп.	Дата	ГД-2026-007-АИ		
						Квартира 65 м²		
						Общая площадь 65,24* м² · * размеры со скана, не замерены (реестр — л. 6–8, К-1)		
Разраб.		Кырлан А.С.			14.11.26	Дизайн-проект интерьера	Стадия: РП	Лист: 1 / Листов: 117
Пров.								
ГИП								
Н. контр.						Титульный лист	Кырлан Александр Сергеевич	
Утв.						М б/м		

выпуск 14.11.2026 № 9cc0b98f36 · стр. 1 из 139

Общие данные

ПРЕДВАРИТЕЛЬНО · не для производства работ · открыто пунктов: 14 (реестр — л. 6–8)

Комплект ГД-2026-007-АИ · Квартира 65 м² после реконструкции

Допущения и предложения на листе. См. лист открытых вопросов (листы 6–8).

Ведомость рабочих чертежей основного комплекта ГД-2026-007-АИ

Лист	Наименование	Примечание
1	Титульный лист	
2	Общие данные	
3	Общие данные	
4	Общие данные	
5	Общие данные	
6	Открытые вопросы, принятые допущения и конфликты. Лист 1 из 3	
7	Открытые вопросы, принятые допущения и конфликты. Лист 2 из 3	
8	Открытые вопросы, принятые допущения и конфликты. Лист 3 из 3	
9	Задание на контрольный обмер и обследование. Лист 1 из 3	
10	Задание на контрольный обмер и обследование. Лист 2 из 3	
11	Задание на контрольный обмер и обследование. Лист 3 из 3	
12	График закупок и работ. Лист 1 из 3	
13	График закупок и работ. Лист 2 из 3	
14	График закупок и работ. Лист 3 из 3	
15	Календарный график работ и закупок	
16	Чек-лист приёмки по этапам. Лист 1 из 4	
17	Чек-лист приёмки по этапам. Лист 2 из 4	
18	Чек-лист приёмки по этапам. Лист 3 из 4	
19	Чек-лист приёмки по этапам. Лист 4 из 4	
20	Лист → мастер	
21	Обмерный план	
22	План демонтажа и монтажа перегородок	
23	План дверей и ведомость заполнения проёмов	
24	Концепция интерьера	
25	План расстановки мебели	
26	Спецификация мебели и оборудования	
27	Спецификация мебели и оборудования (продолжение)	
28	Спецификация мебели и оборудования (продолжение)	
29	План розеток и электровыводов	
30	План освещения	

Ведомость рабочих чертежей основного комплекта ГД-2026-007-АИ (продолжение)

Лист	Наименование	Примечание
31	План выключателей и схема включения	
32	Ведомость электроточек и изделий	
33	Однолинейная схема щита	
34	План принципиальных трасс	
35	Таблица нагрузок щита	
36	План слаботочных сетей	
37	План вентиляции	
38	План отопления	
39	План выводов сантехники	
40	Схема разводки водопровода и канализации	
41	Аксонометрическая схема В1 (холодное водоснабжение)	
42	Аксонометрическая схема Т3 (горячее водоснабжение)	
43	Аксонометрическая схема К1 (канализация)	
44	Развёртки мокрых зон: выводы ВК. Кухня-гостиная	
45	Развёртки мокрых зон: выводы ВК. Санузел	
46	Развёртки мокрых зон: выводы ВК. Ванная	
47	Спецификация сантехнического оборудования	
48	Техническое задание на подбор светильников	
49	План потолков	
50	Разрезы и узлы потолков	
51	Сечения потолков М 1:10	
52	Раскладка плитки. Планы полов	
53	Раскладка плитки. Прихожая. Коридор	

Общие указания — лист 5: ±0,000 — чистый пол; несущие конструкции и сети дома — по отдельному проекту; скрытые работы — по актам. Открытые вопросы и допущения — листы 6–8.

Изм.	Кол.уч	Лист	№ док.	Подп.	Дата
Разраб.		Кырлан А.С.			14.11.26
Пров.					
ГИП					
Н. контр.					
Утв.					

ГД-2026-007-АИ

Квартира 65 м²

Общая площадь 65,24* м² · * размеры со скана, не замерены (реестр — л. 6–8, К-1)

Дизайн-проект интерьера

Стадия	Лист	Листов
РП	2	117

Общие данные

М б/м

Кырлан Александр Сергеевич

выпуск 14.11.2026 № 9cc0b98f36 · стр. 2 из 139

Общие данные

Комплект ГД-2026-007-АИ · лист 2 общих данных (продолжение)

Допущения и предложения на листе. См. лист открытых вопросов (листы 6–8).

Ведомость рабочих чертежей основного комплекта ГД-2026-007-АИ (продолжение)

Лист	Наименование	Примечание
54	Раскладка плитки. Санузел. Развёртки стен	
55	Раскладка плитки. Ванная. Развёртки стен	
56	План полов	
57	Ведомость отделки помещений	
58	Колерная карта	
59	Спецификация отделочных материалов	
60	Спецификация отделочных материалов	
61	Концепция декора и визуализации	
62	План текстиля и декора	
63	Шторы и карнизы	
64	Ведомость текстиля	
65	Ведомость декора	
66	Схемы развески	
67	Встроенная мебель. Схема расположения	
68	Система хранения Г1	
69	Шкаф-купе М11	
70	Система хранения Г2	
71	Шкаф распашной С5	
72	Кухня (пом. 3). Развёртка гарнитура	
73	Кухня (пом. 3). Развёртка гарнитура: вид без фасадов и разрезы	
74	Кухня (пом. 3). Монтажная схема	
75	Кухня (пом. 3). Столешница: план	
76	Шкафы. Монтажная схема	
77	Ведомости изделий, техники и фурнитуры	
78	Сводка листовых материалов и кромки	
79	Реестр марок отделки и позиций альбома	
80	Схема расположения развёрток и узлов	
81	Развёртка стены А. Гардеробная (пом. 1)	
82	Развёртки стен Б, Г. Гардеробная (пом. 1)	
83	Развёртка стены А. Спальня (пом. 2)	

Ведомость рабочих чертежей основного комплекта ГД-2026-007-АИ (продолжение)

Лист	Наименование	Примечание
84	Развёртка стены Б. Спальня (пом. 2)	
85	Развёртки стен В, Г. Спальня (пом. 2)	
86	Развёртка стены В2. Кухня-гостиная (пом. 3), кухонный фронт	
87	Развёртка стены Г. Кухня-гостиная (пом. 3), кухонный фронт	
88	Развёртки стен А1, А2. Кухня-гостиная (пом. 3)	
89	Развёртки стен Б1, Б2, В1. Кухня-гостиная (пом. 3)	
90	Развёртки стен А, Б. Прихожая (пом. 4)	
91	Развёртка стены Г. Прихожая (пом. 4)	
92	Развёртки стен А, Б. Коридор (пом. 5)	
93	Развёртки стен В, Г. Коридор (пом. 5)	
94	Развёртки стен А, Б. Санузел (пом. 6)	
95	Развёртки стен В, Г. Санузел (пом. 6)	
96	Развёртки стен А, Б. Ванная (пом. 7)	
97	Развёртки стен В, Г. Ванная (пом. 7)	
98	Развёртки стен. Кладовая (пом. 8)	
99	Развёртка стены А. Детская (пом. 9)	
100	Развёртка стены Б. Детская (пом. 9)	
101	Развёртка стены В. Детская (пом. 9)	
102	Развёртка стены Г. Детская (пом. 9)	
103	Узлы	
104	Ведомость объёмов работ	
105	Ведомость объёмов работ (продолжение)	
106	Ведомость объёмов работ (окончание)	

Общие указания — лист 5: ±0,000 — чистый пол; несущие конструкции и сети дома — по отдельному проекту; скрытые работы — по актам. Открытые вопросы и допущения — листы 6–8.

Изм.	Кол.уч	Лист	№ док.	Подп.	Дата	ГД-2026-007-АИ		
						Квартира 65 м²		
						Общая площадь 65,24* м² · * размеры со скана, не замерены (реестр — л. 6–8, К-1)		
Разраб.		Кырлан А.С.			14.11.26	Дизайн-проект интерьера	Стадия	Лист	Листов
Пров.							РП	3	117
ГИП						Общие данные	Кырлан Александр Сергеевич		
						М б/м			
Н. контр.									
Утв.									

выпуск 14.11.2026 № 9cc0b98f36 · стр. 3 из 139

Общие данные

Комплект ГД-2026-007-АИ · лист 3 общих данных (продолжение)

Ведомость рабочих чертежей основного комплекта ГД-2026-007-АИ (продолжение)

Лист	Наименование	Примечание
107	Спецификация материалов	
108	Спецификация материалов (окончание)	
109	Смета ориентировочная	
110	Смета ориентировочная (окончание)	
111	Смета проекта: этапы, помещения, итог	
112	Смета проекта: этапы, помещения, итог (продолжение)	
113	Смета проекта: этапы, помещения, итог (окончание)	
114	Смета материалов с ценами	
115	Смета материалов с ценами (продолжение)	
116	Смета материалов с ценами (продолжение)	
117	Смета материалов с ценами (окончание)	

Ведомость ссылочных и прилагаемых документов

Обозначение	Наименование	Примечание
	Ссылочные документы	
ГОСТ 21.201-2011	СПДС. Условные графические изображения элементов зданий, сооружений и конструкций	
ГОСТ 21.205-2016	СПДС. Условные обозначения элементов санитарно-технических систем	
ГОСТ 21.210-2014	СПДС. Изображения условные графические электрооборудования и проводок на планах	
ГОСТ 2.306-68	ЕСКД. Обозначения графические материалов и правила их нанесения на чертежах	
	Прилагаемые документы	
ГД-2026-007-АИ.В1	Визуализация. Вид сверху (3D): планировка с мебелью, текстилем и декором	альбом визуализаций
ГД-2026-007-АИ.В2	Визуализация. Потолок: Ванная (пом. 7)	
ГД-2026-007-АИ.В3	Визуализация. Потолок: Спальня (пом. 2)	
ГД-2026-007-АИ.В4	Визуализация. Потолок: Коридор (пом. 5)	
ГД-2026-007-АИ.В5	Визуализация. Потолок: Прихожая (пом. 4)	
ГД-2026-007-АИ.В6	Визуализация. Потолок: Детская (пом. 9)	
ГД-2026-007-АИ.В7	Визуализация. Потолок: Кухня-гостиная (пом. 3)	
ГД-2026-007-АИ.В8	Визуализация. Потолок: Санузел (пом. 6)	
ГД-2026-007-АИ.В9	Визуализация. Интерьер: Ванная (пом. 7), общий вид	
ГД-2026-007-АИ.В10	Визуализация. Интерьер: Спальня (пом. 2), стена А	
ГД-2026-007-АИ.В11	Визуализация. Интерьер: Спальня (пом. 2), общий вид	
ГД-2026-007-АИ.В12	Визуализация. Интерьер: Коридор (пом. 5), стена А	
ГД-2026-007-АИ.В13	Визуализация. Интерьер: Прихожая (пом. 4), общий вид	
ГД-2026-007-АИ.В14	Визуализация. Интерьер: Детская (пом. 9), стена В	
ГД-2026-007-АИ.В15	Визуализация. Интерьер: Детская (пом. 9), стена Г	
ГД-2026-007-АИ.В16	Визуализация. Интерьер: Кухня-гостиная (пом. 3), стена А	

Допущения и предложения на листе

Основа листа: размеры сняты с растрового плана заказчика без размеров: масштаб восстановлен по площадям помещений (≈ 11,8 мм на пиксель), контрольный обмер не выполнен (К-1); высота потолка 2700 мм принята: на плане заказчика её нет (К-2); толщины стен 300 / 120 мм приняты по плану заказчика, не замерены (К-1); разрешённая мощность 15 кВт принята по типовым ТУ для квартиры, ТУ заказчиком не переданы (К-4); подрайон климата не задан — принят не северный (жилые от 2,5 м) (К-9).
См. лист открытых вопросов (лист 6, записи К-1, К-2, К-4; лист 7, запись К-9).

Общие указания — лист 5: ±0,000 — чистый пол; несущие конструкции и сети дома — по отдельному проекту; скрытые работы — по актам. Открытые вопросы и допущения — листы 6–8.

Изм.	Кол.уч	Лист	№ док.	Подп.	Дата
Разраб.		Кырлан А.С.			14.11.26
Пров.					
ГИП					
Н. контр.					
Утв.					

ГД-2026-007-АИ

Квартира 65 м²

Общая площадь 65,24* м² · * размеры со скана, не замерены (реестр — л. 6–8, К-1)

Дизайн-проект интерьера

Стадия	Лист	Листов
РП	4	117

Общие данные

М б/м

Кырлан Александр Сергеевич

выпуск 14.11.2026 № 9cc0b98f36 · стр. 4 из 139

Общие данные

Комплект ГД-2026-007-АИ · лист 4 общих данных (продолжение)

Ведомость ссылочных и прилагаемых документов (продолжение)

Обозначение	Наименование	Примечание
ГД-2026-007-АИ.В17	Визуализация. Интерьер: Кухня-гостиная (пом. 3), общий вид	
ГД-2026-007-АИ.В18	Визуализация. Интерьер: Гардеробная (пом. 1), общий вид	
ГД-2026-007-АИ.В19	Визуализация. Интерьер: Санузел (пом. 6), общий вид	

Состав дизайн-проекта

Раздел	Состав	Листы
Обложка	Дизайн-проект интерьера; Квартира 65 м²; автор проекта — Кырлан Александр Сергеевич	1 с.
Концепция	Стиль Скандинавский: концепция интерьера, палитра и материалы (колерная карта лист 58)	л. 24
Визуализации	19 изобр.: Вид сверху (3D): планировка с мебелью, текстилем и декором; Потолок: Ванная; Потолок: Спальня; Потолок: Коридор; Потолок: Прихожая; Потолок: Детская; Потолок: Кухня-гостиная; Потолок: Санузел; Ванная, общий вид; Спальня, стена А; Спальня, общий вид; Коридор, стена А; Прихожая, общий вид; Детская, стена В; Детская, стена Г; Кухня-гостиная, стена А; Кухня-гостиная, общий вид; Гардеробная, общий вид; Санузел, общий вид	В1–В19
Рабочие чертежи	планы, развёртки, узлы (развёртки и узлы — листы 44–46, 80, 82, 85, 88–90, 92–98, 103)	л. 1–117
Спецификации и ведомости	оборудование, изделия, отделка, электроточки	л. 23, 26–28, 32, 47, 57–60, 64, 65, 104–108

Условные обозначения

- контрольный отрезок 1000 мм натуры: по нему проверяют печать 1:1
- отметка уровня, м: ±0,000 — чистый пол жилых помещений
- А — марка развёртки: буква стены, стрелка — взгляд
- О1 — марка отделки по реестру отделки альбома
- выноска узла: над полкой — узел, под полкой — лист

Допущения и предложения на листе

Основа листа: размеры сняты с растрового плана заказчика без размеров: масштаб восстановлен по площадям помещений (≈ 11,8 мм на пиксель), контрольный обмер не выполнен (К-1); высота потолка 2700 мм принята: на плане заказчика её нет (К-2); толщины стен 300 / 120 мм приняты по плану заказчика, не замерены (К-1); разрешённая мощность 15 кВт принята по типовым ТУ для квартиры, ТУ заказчиком не переданы (К-4); подрайон климата не задан — принят не северный (жилые от 2,5 м) (К-9).
См. лист открытых вопросов (лист 6, записи К-1, К-2, К-4; лист 7, запись К-9).

Общие указания

1. Рабочие чертежи интерьера разработаны на основании задания на проектирование и обмерного плана (лист 21). Объект: Квартира 65 м²; автор проекта — Кырлан Александр Сергеевич; общая площадь 65,24 м², жилая 43,2 м², помещений 9.
2. Рабочие чертежи выполнены в соответствии с заданием на проектирование и нормативными документами, перечисленными в п. 4.
3. Открытые вопросы, принятые допущения и конфликты между разделами, не снятые к выпуску комплекта, сведены в таблицы на листах 6–8. До ответа по пункту таблицы показанное на указанном там листе — допущение, а не утверждённое решение: комплект по этим листам предварительный.
4. Нормативные документы, на которые есть ссылки в листах комплекта: ГОСТ Р 21.101-2026; ГОСТ 21.501-2018; ГОСТ 2.302-68; ГОСТ 2.303-68; ГОСТ 2.304-81; ГОСТ 2.307-2011; СП 54.13330.2022; СП 71.13330.2017; СП 73.13330.2016; ПУЭ (7-е изд.), гл. 1.8, 7.1; ГОСТ Р 50571.7.701-2024; СанПиН 1.2.3685-21; ГОСТ 2.702; ГОСТ 2.755; ГОСТ 21.110-2013; ГОСТ 21.601; ГОСТ 13996-2019; ГОСТ 23166-2021; ГОСТ 31173-2016; ГОСТ 31565-2012; ГОСТ 32414-2013; ГОСТ 32415-2013; ГОСТ Р 56387-2018; СП 29.13330.2011; СП 30.13330.2020; СП 51.13330.2011; СП 131.13330; СП 163.1325800.2014; СП 256.1325800.2016. Документы из ведомости ссылочных документов здесь не повторяются.
5. За отметку ±0,000 принят уровень чистого пола жилых помещений квартиры (относительная отметка; абсолютная — по проекту дома).
6. Несущие конструкции, общедомовые стояки, вентиляционные каналы и инженерные сети дома настоящим комплектом не изменяются. Работы, затрагивающие их (проём или штраба в несущей стене, перенос стояка, врезка в вентканал, расширение мокрой зоны), выполняются только по отдельному проекту, к которому прилагается техническое заключение о допустимости и безопасности работ, выданное автором проекта дома или организацией с допуском на обследование, и который согласован в установленном порядке (Жилищный кодекс РФ, ст. 25–29).
7. Трассы инженерных сетей на листах — принципиальные. Расчёты электрических нагрузок и токов КЗ, гидравлики, воздухообмена, освещённости и нагрузок на перекрытие выполняются в проектах ЭОМ, ВК, ОВ и КР организацией с допуском СРО; фактические трассы до закрытия отделкой фиксируются исполнительными схемами.
8. Стиль интерьера — Скандинавский. Палитра проекта: основной — NCS S 1502-Y50R «S 1502-Y50R», NCS S 1002-Y50R «S 1002-Y50R», NCS S 0300-N «S 0300-N», Tikkurila V503 «Winter»; дополнительный — Farrow & Ball No. 241 «Skimming Stone», NCS S 0502-Y «S 0502-Y»; акцент — Farrow & Ball No. 30 «Hague Blue». Коды цвета — по веерам производителей; цвет утверждается по выкрасу на объекте при освещении проекта.
9. Площади поверхностей — по чистым граням стен до отделки: стены = периметр × высоту от чистого пола помещения до низа потолка минус проёмы (облицовка плиткой — до верха облицовки); плинтус = периметр минус дверные проёмы; пол и потолок — по площади помещения. Количество плиток — по раскладке. Способ один для всех листов комплекта (ведомость отделки, колерная карта, раскладка плитки, развёртки).
10. Марки: стены помещения на всех листах — А (верхняя по плану), Б (правая), В (нижняя), Г (левая); марка отделки О — одна на весь альбом; реестр марок отделки (с позициями колерной карты той же отделки) и марки позиций по видам — на листе 79.
11. Развёртки стен выполнены по всем помещениям для стен с электроточками, мебелью, декором и отделкой: санузлы и кухонный фронт — в М 1:25, остальные стены — в М 1:25; расположение развёрток и узлов — на листе 80, узлы — на листе 103.
12. Перечень скрытых работ, на которые составляются акты освидетельствования (форма по приказу Минстроя России № 344/пр): гидроизоляция пола и стен мокрых помещений (с тестом проливом); стяжка пола (толщина, прочность, влажность основания); тёплый пол до заливки (сопротивление, схема укладки); скрытая электропроводка (за потолком и в штробах стен; условия штробления — в следующем пункте); трубопроводы водоснабжения и канализации до закрытия (опрессовка, уклоны); закладные и усиления под подвесные приборы, мебель и тяжёлый декор, рамы инсталляций; короба дверей скрытого монтажа до штукатурки; каркасы ГКЛ потолков, коробов и перегородок до обшивки.
13. Скрытая электропроводка: за потолком и в штробах стен. Штробы в стенах выполняются только после технического заключения о несущих конструкциях; до заключения несущие стены не определены, и все стены считаются несущими; объём штроб — в ведомости объёмов работ, строка «Штробы в стенах» (вертикальные спуски; объём не меньше фактического, горизонтальные трассы — по исполнительной схеме).
14. Критерии приёмки: допуски отделочных покрытий — по СП 71.13330.2017; испытания систем водоснабжения и канализации — по СП 73.13330.2016 до закрытия трасс; приёмо-сдаточные испытания электроустановки — по ПУЭ, гл. 1.8, с протоколом электролаборатории.
15. Осознанные отступления от ГОСТ Р 21.101-2026, принятые в комплекте: номер листа и число листов («Листов») указаны на каждом листе; на масштабных листах в основной надписи указан фактический масштаб и дан контрольный отрезок 1000 мм; развёртки стен выполнены в М 1:25 (ГОСТ 21.507-81 — 1:50…1:500) ради читаемости привязок; размерные числа и марки элементов (Д-1, ОК-1, О6) кеглем 2,5 мм, номера помещений — в кружке Ø 8 мм (канон — 3,5 мм и Ø 12 мм): так насыщенные листы А3 читаются без наложений надписей.
16. Графы «Пров.», «Н. контр.», «Утв.» основной надписи заполняются при согласовании комплекта с заказчиком; до согласования комплект подписывает автор проекта (графа «Разраб.»).

Изм.	Кол.уч	Лист	№ док.	Подп.	Дата	ГД-2026-007-АИ		
						Квартира 65 м²		
						Общая площадь 65,24* м² · * размеры со скана, не замерены (реестр — л. 6–8, К-1)		
Разраб.		Кырлан А.С.			14.11.26	Дизайн-проект интерьера	Стадия: РП	Лист: 5 / Листов: 117
Пров.								
ГИП								
Н. контр.						Общие данные	Кырлан Александр Сергеевич	
Утв.						М б/м		

выпуск 14.11.2026 № 9cc0b98f36 · стр. 5 из 139

Открытые вопросы, принятые допущения и конфликты. Лист 1 из 3

ПРЕДВАРИТЕЛЬНО · не для производства работ · открыто пунктов: 14 (реестр — л. 6–8)

Сводка по реестрам координации (стартовое совещание 09.10.2026)

Комплект предварительный по пунктам этих таблиц. Пока по пункту нет ответа или решения, показанное на указанном листе — допущение проектировщика, а не утверждённое решение.
Сводка: открытых вопросов — 12 (из них ждут факта объекта — 5: контрольного обмера, обследования или документа); изменений в реестре — 5, из них без подписи — 2.
Пункты, ответ на которые лежит на объекте, а не за столом проектировщика (графа «Вид», строка «Ждёт»), собраны на листе «Задание на контрольный обмер и обследование» (листы 9–11): что и где замерить, с какой точностью и чем подтвердить. Пункты, ждущие решения человека, на объекте не закрываются.

Открытые вопросы и принятые допущения

№	Формулировка	Вид	Кто решает	Если решения нет	Лист, где это проявляется
К-1	Размеры квартиры сняты с растрового плана заказчика без размерных цепочек: масштаб восстановлен по подписанным площадям помещений. До заказа мебели, дверей и материалов нужен контрольный обмер всех помещений и проёмов.	Отсутствует Ждёт: обмера	Архитектор-планировщик	размеры на листах — по плану заказчика, уточняются по месту; мебель на заказ и материалы по ним не заказывать	л. 21 — Обмерный план л. 25 — План расстановки мебели
К-2	Высота потолка на плане заказчика не указана, принята 2700 мм.	Отсутствует	Архитектор-планировщик	высоты на развёртках и потолки — от 2700 мм, уточнить при обмере	л. 21 — Обмерный план л. 49 — План потолков
К-4	Разрешённая мощность квартиры по ТУ неизвестна, принята 15 кВт.	Отсутствует	Инженер-электрик	щит и группы рассчитаны на 15 кВт; при меньших ТУ пересчёт	л. 33 — Однолинейная схема щита л. 29 — План розеток и электровыводов
К-5	Кухня-гостиная (пом. 3): диван М1 2200 × 950 стоит в полосе 1400 мм между спальней и кухней — единственном проходе от двери из коридора в комнату; за спинкой остаётся щель 290 мм, в выпуске для заказчика это ошибка. Полоса годится только под проход и неглубокую мебель (до 700 мм). В основной части (2700 × 2900 мм) диван, обеденная группа на 4 места, рабочее место С4 и кресло М3 вместе с проходами не помещаются. Нужно решение по составу зоны: (1) диван в основную часть лицом к ТВ на стене Г, обеденный стол — в нишу у колонны М8, рабочее место С4 — в спальню или детскую; (2) диван двухместный 1600 мм у стены спальни в основной части; (3) вместо обеденной группы — барная стойка. До решения расстановка кухни-гостиной не годится для заказа мебели. Решение исполнителя (ИЗ-1, 30.10.2026, на утверждение автора): вариант 1 без переноса рабочего места — диван М1 у стены А основной части (х 250…2450, у 1650…2600), обеденный стол М2 перед ним (х 1100…2100, у 2800…3800), кресло М3 у окна 2 (х 400…1150, у 3700…4450), ТВ остаётся на стене Г; полоса 1400 у спальни свободна под проход; части 2–4 помещения перекроены (кухонный ряд и ниша — одна часть) без изменения контура. Стыки частей ≥ 700 мм.	Спорно Ждёт: решения	Дизайнер интерьера	расстановка М1, М2, М3 остаётся предложением со знаком «**»: мебель кухни-гостиной не заказывать до подписи ИЗ-1	л. 25 — План расстановки мебели
К-6	Спальня (пом. 2) без окна (К-3): приток не решён — бризер на внутренней стене Б не работает (нужно отверстие в наружной стене), а наружная стена А занята изголовьем кровати С1 (бризер над кроватью — холодный поток на спящего). Радиатор Р-2 оставлен на стене Б у двери. После решения по окну: бризер или клапан — у окна, радиатор — под окно; если помещение станет нежилым приток не нужен.	Решение	Инженер ОВ	приток в спальню не обеспечен: на плане вентиляции «!» в графе притока; радиатор Р-2 — на стене Б	л. 37 — План вентиляции л. 38 — План отопления
К-7	Вентканалы на плане заказчика не показаны: ВК-1 и ВК-2 приняты проектировщиком у кухни, ванная (пом. 7) от них далеко вытяжка ВР3 идёт воздуховодом ≈ 4 м через санузел. Замерить положение и сечение каналов; если канал у ванной есть — решётку в его стенку, воздуховод не нужен.	Отсутствует Ждёт: обмера	Инженер ОВ	вытяжка ванной — вентилятором с обратным клапаном и воздуховодом под потолком до ВК-2; места решёток — до обмера	л. 37 — План вентиляции

Изм.	Кол.уч	Лист	№ док.	Подп.	Дата
Разраб.		Кырлан А.С.			14.11.26
Пров.					
ГИП					
Н. контр.					
Утв.					

ГД-2026-007-АИ

Квартира 65 м²

Общая площадь 65,24* м² · * размеры со скана, не замерены (реестр — л. 6–8, К-1)

Дизайн-проект интерьера

Стадия	Лист	Листов
РП	6	117

Открытые вопросы, принятые допущения и конфликты. Лист 1 из 3
М б/м

Кырлан Александр Сергеевич

выпуск 14.11.2026 № 9cc0b98f36 · стр. 6 из 139

Открытые вопросы, принятые допущения и конфликты. Лист 2 из 3

Сводка по реестрам координации (стартовое совещание 09.10.2026)

Открытые вопросы и принятые допущения (продолжение)

№	Формулировка	Вид	Кто решает	Если решения нет	Лист, где это проявляется
К-8	Проём санузла (пом. 6, марка Д-5) по плану заказчика 550×2100 — уже ряда стандартных полотен (600–900): полотно ≈ 450 под заказ, проход меньше 600. Откос от угла коридора до проёма — 40 мм, под коробку нужно не меньше 50. Проём в существующей стене: расширить до 700 (полотно 600) можно только при подтверждении, что стена не несущая (техзаключение / план БТИ). Замерить проём в чистоте и откос; решить — расширение по техзаключению или изделие под заказ.	Спорно Ждёт: обмера, затем решения	Архитектор-планировщик	Д-5 — скрытая дверь под заказ по проёму 550×2100 (полотно ≈ 450), проём не расширяется; заказ — только после замера в чистоте	л. 23 — План дверей и ведомость заполнения проёмов
К-9	Климатический подрайон (СП 131.13330) не задан: принят не северный — жилые комнаты и кухня под потолком от 2,5 м (СП 54, п. 5.12); в IA, IБ, IГ, IД, IVA — от 2,7 м.	Отсутствует Ждёт: документа	Архитектор-планировщик	отметки потолков жилых — по 2,5 м; при северном подрайоне уровни ниже 2,7 м пересчитать до заказа каркаса	л. 49 — План потолков
К-10	Несущие стены не определены: плана БТИ, проекта дома и технического заключения в материалах объекта нет. До их получения все существующие стены считаются несущими — демонтаж, новые проёмы и штробы в них не планируются. Нужно: запросить план БТИ и проект дома, установить серию и материал стен; несущие стены и допустимость вмешательства определяет техническое заключение специализированной организации.	Отсутствует Ждёт: документа	Архитектор-планировщик	все существующие стены — несущие: перепланировка и штробы в них не выполняются, на листах обмера и демонтажа — «не определены, считать несущими»	л. 21 — Обмерный план л. 22 — План демонтажа и монтажа перегородок
К-12	Циркуляция ГВС в данных не задана — циркуляционного трубопровода на схеме нет. Решить: нужна ли циркуляция	Отсутствует Ждёт: решения	Инженер ВК (вода, канализация)	циркуляции на схеме нет	л. 44–46 — Развёртки мокрых зон: выводы ВК. Кухня-гостиная л. 41 — Аксонометрическая схема В1 (холодное водоснабжение) л. 40 — Схема разводки водопровода и канализации
К-13	Помещение «Гардеробная»: выключатель основного света L6 (S1) не у входа — у двери Д-3 со стороны ручки свободного места нет (проём в 100 мм от угла, мебель у двери, чужие точки или выключатель общий с соседним помещением; расстановка мебель и двери не двигает). Варианты: (а) петли на другую сторону — ручка уходит от угла, выключатель встаёт у ручки; (б) шкаф или тумбу у двери сдвинуть на 300 мм — место освобождается; (в) беспроводной выключатель на клее у ручки (реле в подрозетнике ближней стены) — по согласованию с заказчиком; (г) оставить как есть (S1): рука дальше 350 мм от ручки.	Спорно Ждёт: решения	Инженер-электрик	выключатель L6 остаётся на месте (S1); закладные под выключатель у двери не делать до решения	л. 31 — План выключателей и схема включения
К-14	Помещение «Коридор»: выключатель основного света L3 (S3, S5) не у входа — у двери А 150, Д-2, Д-2, Д-5, Д-4 со стороны ручки свободного места нет (проём в 100 мм от угла, мебель у двери, чужие точки или выключатель общий с соседним помещением; расстановка мебель и двери не двигает). Варианты: (а) петли на другую сторону — ручка уходит от угла, выключатель встаёт у ручки; (б) шкаф или тумбу у двери сдвинуть на 300 мм — место освобождается; (в) беспроводной выключатель на клее у ручки (реле в подрозетнике ближней стены) — по согласованию с заказчиком; (г) оставить как есть (S3, S5): рука дальше 350 мм от ручки.	Спорно Ждёт: решения	Инженер-электрик	выключатель L3 остаётся на месте (S3, S5); закладные под выключатель у двери не делать до решения	л. 31 — План выключателей и схема включения

						ГД-2026-007-АИ	
						Квартира 65 м²	
Изм.	Кол.уч	Лист	№ док.	Подп.	Дата	Общая площадь 65,24* м² · * размеры со скана, не замерены (реестр — л. 6–8, К-1)	
Разраб.		Кырлан А.С.			14.11.26	Дизайн-проект интерьера	Стадия: РП; Лист: 7; Листов: 117
Пров.							
ГИП							
Н. контр.						Открытые вопросы, принятые допущения и конфликты. Лист 2 из 3 М б/м	Кырлан Александр Сергеевич
Утв.							

выпуск 14.11.2026 № 9cc0b98f36 · стр. 7 из 139

Открытые вопросы, принятые допущения и конфликты. Лист 3 из 3

Сводка по реестрам координации (стартовое совещание 09.10.2026)

Изменения проекта после выпуска листов (реестр изменений)

№	Дата	Лист	Было	Стало	Кто решил, подпись
ИЗ-1	30.10.2026	л. 25 — План расстановки мебели л. 26 — Спецификация мебели и оборудования л. 29 — План розеток и электровыводов л. 86 — Развёртка стены В2. Кухня-гостиная (пом. 3), кухонный фронт	Кухня-гостиная (пом. 3): диван М1 2200×950 стоял в полосе 1400 мм между спальней и кухней (x 2900…5100, y 3000…3950) — единственном проходе от двери Д-2; стыки частей 0–1 — 290 мм, 1–3 — 200, 1–4 — 0, 2–3 — 600; кресло М3 в x 800, стол М2 в x 1000, y 2700. Вопрос К-5 открыт.	Диван М1 у стены А основной части (x 250…2450, y 1650…2600), стол М2 перед ним (x 1100…2100, y 2800…3800), кресло М3 у окна 2 (x 400…1150, y 3700…4450); розетки «у дивана» перенесены на стену А (x 700, 2300), розетка торшера — на стену Г (смещение 1900). Части помещения 2–4 перекроены без изменения контура: кухонный ряд М4…М8 и ниша С4 — одна часть (0…4850 × 4550…5800), связка 2700…4850 × 4050…4550; стык частей 2–3 проходил сквозь кухонный ряд (600 мм — глубина столешницы, не проход). Знак «**» у М1, М2, М3 до подписи автора; К-5 — у автора.	Утверждено: Кырлан А.С., 12.11.2026. Предложил: исполнитель.
ИЗ-2	10.11.2026	л. 25 — План расстановки мебели л. 29 — План розеток и электровыводов	Диван М1 стоял на y 1700 мм, а чистая грань стены А помещения — на y 1710; розетка «у дивана» на стене А (смещение 200 мм, высота 300) — в 50 мм от бока дивана (x 250), закрыта мебелью.	Диван М1 — y 1710 мм (было 1700), по чистой грани стены А: x 250…2450, y 1710…2660; размеры 2200 × 950 мм и положение по x прежние. Розетка «у дивана» на стене А — смещение 150 мм (было 200), высота 300 мм прежняя: 100 мм до бока дивана, 150 мм до угла. Вторая розетка у дивана (смещение 2550) не тронута. Диван остаётся предложением (ИЗ-1, К-5).	Утверждено: Кырлан А.С., 12.11.2026. Предложил: исполнитель.
ИЗ-3	11.11.2026	л. 21 — Обмерный план л. 23 — План дверей и ведомость заполнения проёмов л. 83 — Развёртка стены А. Спальня (пом. 2) л. 25 — План расстановки мебели л. 29 — План розеток и электровыводов	Спальня (пом. 2, x 2700…6000, y 0…2650) выходила на наружную стену А (фасад, y = 0, как гардеробная и верхний край контура), но окна в ней не было: жилая комната без естественного освещения.	В наружной стене А спальни добавлено окно: смещение от левого угла стены 1400 мм, ширина 1400, высота 1600, подоконник 800 (тот же тип и размеры по высоте, что у окон кухни-гостиной и детской). Проём 1400…2800 лежит над изголовьем кровати С1 (850…2450) и тумбой С2 не задевает; бра L8 (смещения 1025 и 3150), розетки (1050, 3150) и выключатель S6 (1250) остаются вне проёма. Радиатор Р-2 остаётся на стене Б (под изголовьем кровати радиатор не ставится). Мебель не двигалась. Вопрос К-3 закрыт; приток воздуха (К-6) теперь решается клапаном или бризером в наружной стене рядом с окном, после обмера и утверждения.	Утверждено: Кырлан А.С., 12.11.2026. Предложил: исполнитель.
ИЗ-4	12.11.2026	л. 62 — План текстиля и декора л. 64 — Ведомость текстиля л. 65 — Ведомость декора л. 63 — Шторы и карнизы	Декор и текстиль были заданы только в детской (пом. 9). В кухне-гостиной, спальне, прихожей, коридоре и санузлах не было ни штор, ни ковров, ни подушек и пледов, ни картин, зеркал и растений; кадры визуализаций и листы декоратора строятся только по данным — помещения выходили пустыми. В детской подушки и плед (Т10–Т12) были записаны «на С7» (это стол), у картины ДК3 не было сюжета.	Декор и текстиль заданы позициями плана. Кухня-гостиная: римские шторы на оба окна (Т1, Т2; в пол не идут — под окнами радиаторы, диван в 250 мм от окна 1), подушки 3 + 2 и плед на диван М1 (Т3–Т5), картина 1400×900 над диваном на стене А (ДК1; низ 1050), сансевиерия в напольном кашпо у рабочего места (ДК2), ваза на обеденном столе М2 (ДК5). Спальня: римская штора с блэкаутом на окно над изголовьем (Т6), ковёр 2500×1250 под кроватью с выходом по 450 мм по бокам, вне зоны открывания двери Д-3 (Т13), подушки 2 + 1 и плед на кровать С1 (Т14–Т16), картина 1000×700 на стене В напротив кровати (ДК6), зеркало в рост 500×1600 на стене Г у двери гардеробной (ДК7). Прихожая: дорожка 800×1400 (Т17), зеркало в рост 500×1600 на стене Г (ДК8). Коридор: три постера 400×560 в дубовых рамах на глухой стене А, шаг между рамами 70 мм (ДК9–ДК11). Санузел и ванная: зеркала над умывальниками П21 и П3 (ДК12, ДК13). Детская: подушки и плед Т10–Т12 — на кровать С6 (было «С7» — стол), картине ДК3 задан сюжет. Цвета — из палитры стиля: молочный, каменный, акценты — приглушённый синий Farrow & Ball No. 299 и терракота NCS S 3020-Y80R. Ковёр в кухне-гостиной не задан: обеденный стол М2 стоит в 140 мм от дивана, ковёр под столом с выходом 600 мм не помещается; дорожка в коридоре не задана пол в зонах открывания четырёх дверей. Знак «**» у позиций до подписи автора.	Не утверждено: подписи нет. решение исполнителя; предложение проектировщика, на утверждение А. С. Кырлана
ИЗ-5	12.11.2026	л. 62 — План текстиля и декора л. 64 — Ведомость текстиля л. 65 — Ведомость декора	Разбор двух критиков по кадрам: мокрые зоны — «стерильный шоурум»: в ванной на полотенцесушителе П5 нет полотенец, у ванны нет коврика; в санузле, кроме зеркала, ничего нет (ИЗ-4 задал там только зеркала). Замечание «ванна без смесителя» по данным не подтверждается: у П1 записано «смеситель настенный» — это расхождение кадра, а не данных.	Ванная: банные полотенца приглушённого синего и ручные молочные на полотенцесушителе П5 (Т18, Т19), коврик 600×450 у бортика ванны (Т20; вне полотна двери Д-4 и перед умывальником П3). Санузел: постер 300×400 на стене Г (ДК14); полки короба инсталляции в данных санузла нет — предметы на полку не заданы. Прихожая и коридор не дополнялись: зеркало, дорожка и триптих заданы ИЗ-4, свободных простенков нет. Знак «**» у позиций до подписи автора.	Не утверждено: подписи нет. решение исполнителя; предложение проектировщика, на утверждение А. С. Кырлана

Примечания

1. Номера листов — по ведомости рабочих чертежей комплекта (лист «Общие данные»).
2. Графа «Если решения нет» показывает состояние решения на листах; влияние на сроки и стоимость по пунктам не оценивалось.
3. Пункт, по которому принято решение, при следующем выпуске комплекта из таблиц исключается.

Изм.	Кол.уч	Лист	№ док.	Подп.	Дата
Разраб.		Кырлан А.С.			14.11.26
Пров.					
ГИП					
Н. контр.					
Утв.					

ГД-2026-007-АИ

Квартира 65 м²

Общая площадь 65,24* м² · * размеры со скана, не замерены (реестр — л. 6–8, К-1)

Дизайн-проект интерьера

Стадия	Лист	Листов
РП	8	117

Открытые вопросы, принятые допущения и конфликты. Лист 3 из 3
М б/м

Кырлан Александр Сергеевич

Задание на контрольный обмер и обследование. Лист 1 из 3

ПРЕДВАРИТЕЛЬНО · не для производства работ · открыто пунктов: 14 (реестр — л. 6–8)

Что замерить, вскрыть и получить до заказа материалов и изделий

Задание собрано из открытых вопросов, ответ на которые лежит на объекте или в документах, а не за столом проектировщика. Пока факт не получен, размер, материал или положение на листах — допущение (знак «*»), а не замер.
Сводка: на объекте — 10 (до демонтажа — 8; после демонтажа — 2); документом и при закупке — 3; из допущений в данных и на листах — 9, из них без вопроса в реестре — 5. Закрываются вопросы: К-1, К-2, К-4, К-7–К-10 (7). Вопросы, ждущие решения человека, задание не закрывает — они решаются по реестру открытых вопросов.

Условия проведения

Порядок работ	Приёмы и точность	Кто присутствует	Если факт не совпал с проектом
1. До демонтажа — существующее состояние: контур, диагонали, высоты, проёмы, оси стояков, ниши и конструкции, которые видны. 2. После демонтажа, до черновых работ — то, что закрывали отделка и короба: основание стен, фактические толщины, углы, узлы. 3. Документы и данные закупки — не на объекте: к сроку из последней таблицы, от них зависят привязки и заказ. Что заказывается по размеру из задания, до закрытия пункта не заказывают: сроки изготовления — по графику закупок прораба.	Обход по часовой стрелке от входа: стены, проёмы, потолок, коммуникации (стояки, щиток, вентканалы), особенности (ниши, короба, выступы). Размеры записывают в мм; сумма участков равна общему размеру, при цепочке длиннее трёх участков ставят проверочный (общий) размер. Диагонали каждого помещения; если две диагонали различаются на 5 мм и больше, разницу подписывают на плане. Потолок — в нескольких точках: центр, углы, у проёмов. Проём — ширина, высота, глубина откоса, привязка к ближайшим углам, высота подоконника. Допустимая погрешность прибора — 2–3 мм на метр; размеры округляют кратно 5 мм; два контрольных промера одного размера не должны расходиться более чем на 2 %. Допуск по пункту — в графе «Точность». План БТИ обмер не заменяет.	Прораб (отвечает за проведение) — назначает день и порядок обхода, открывает объект и освобождает помещения, ведёт это задание и реестр изменений. Архитектор — выполняет обмер, составляет акт контрольного обмера и подписывает результаты по размерам и конструкциям. Владельцы вопросов присутствуют при пунктах своего раздела или принимают результат до заказа: Инженер ОВ — К-7; позиции О-3; Инженер ВК (вода, канализация) — позиции О-1; Инженер-электрик — К-4; позиции О-2; Отделочник — позиции О-9, О-10. Заказчик или его представитель — передаёт документы (план БТИ, проект дома, технические условия, паспорта), подписывает акт. Проектных решений на обмере не принимают: обмер даёт факт, решения — по реестру открытых вопросов (листы 6–8).	1. В пределах допуска пункта — принимается измеренное значение, лист перевыпускается, знак «*» снимается. 2. Больше допуска или контрольные промеры расходятся более чем на 2 % — промер повторяют; не подтвердилось — запись в реестр изменений (дата, лист, было, стало, кто решил, подпись), работы в этом месте не начинают. 3. Затронуты несущая стена, стояк, вентканал или мокрая зона — сразу владельцу раздела и ГИПу (главному инженеру проекта); между разделами не больше двух кругов, затем решает ГИП. 4. На объекте устно ничего не согласуется: каждое решение — записью в реестр с подписью.

Этап 1. До демонтажа

№	Где	Способ	Что сделать	Кто выполняет	Точность	Что пересчитается в альбоме	Чем подтверждается	Закрывает вопросы реестра
О-1	Ввод В1 и Т3** у стояков; по всей квартире	Обмер	Отключающая арматура и счётчики воды на вводах: положение, тип, пломбы управляющей компании. Альбом ставит их на каждом вводе по практике, в данных их нет.	Архитектор	±5 мм	Узлы ввода в спецификации ВК (краны, фильтры, счётчики); места ввода на плане выводов. Листы: л. 39 — План выводов сантехники л. 47 — Спецификация сантехнического оборудования	акт контрольного обмера; фото с рулеткой и привязкой к стене или углу	Вопроса в реестре нет: Альбом принимает счётчики воды на вводах без осмотра. Результат принимает: Инженер ВК (вода, канализация)
О-2	Вход в квартиру или лестничная клетка; место щита на плане	Обмер	Существующий щиток и счётчик электроэнергии: место и габарит ниши, состояние ввода, марка и сечение вводного кабеля, наличие вводного автомата и УЗО, пломбы.	Архитектор	±5 мм	Ниша и место щита на листах; вводной кабель и аппараты на однолинейной схеме; расстояния до первых групп. Листы: л. 33 — Однолинейная схема щита	акт контрольного обмера; фото с рулеткой и привязкой к стене или углу	Вопроса в реестре нет: Альбом принимает щит и ввод без осмотра. Результат принимает: Инженер-электрик

Допущения и предложения на листе
Основа листа: размеры сняты с растрового плана заказчика без размеров: масштаб восстановлен по площадям помещений (≈ 11,8 мм на пиксель), контрольный обмер не выполнен (К-1); высота потолка 2700 мм принята: на плане заказчика её нет (К-2); толщины стен 300 / 120 мм приняты по плану заказчика, не замерены (К-1); разрешённая мощность 15 кВт принята по типовым ТУ для квартиры, ТУ заказчиком не переданы (К-4); подрайон климата не задан — принят не северный (жилые от 2,5 м) (К-9).
Знак «**» — предложение проектировщика, заказчиком не утверждено (согласовать с заказчиком): ИЗ-4: Т3.
См. лист открытых вопросов (лист 6, записи К-1, К-2, К-4; лист 7, запись К-9; лист 8, запись ИЗ-4).

Изм.	Кол.уч	Лист	№ док.	Подп.	Дата
Разраб.		Кырлан А.С.			14.11.26
Пров.					
ГИП					
Н. контр.					
Утв.					

ГД-2026-007-АИ

Квартира 65 м²

Общая площадь 65,24* м² · * размеры со скана, не замерены (реестр — л. 6–8, К-1)

Дизайн-проект интерьера

Стадия	Лист	Листов
РП	9	117

Задание на контрольный обмер и обследование.
Лист 1 из 3
М б/м

Кырлан Александр Сергеевич

выпуск 14.11.2026 № 9cc0b98f36 · стр. 9 из 139

Задание на контрольный обмер и обследование. Лист 2 из 3

Что замерить, вскрыть и получить до заказа материалов и изделий

Этап 1. До демонтажа (продолжение)

№	Где	Способ	Что сделать	Кто выполняет	Точность	Что пересчитается в альбоме	Чем подтверждается	Закрывает вопросы реестра
О-3	у окон	Обмер	Положение стояков отопления (подающий и обратный) от граней стен, диаметры, наличие запорной арматуры; существующие радиаторы: число секций, межосевое расстояние, подводки. В данных стояков отопления нет — лист отопления выводит их условно у откоса окна.	Архитектор	±5 мм	План отопления: места стояков и подводок, привязки радиаторов; подбор радиаторов по теплотехническому расчёту; радиаторы и узлы подключения в ВОР и спецификации. Листы: л. 38 — План отопления	акт контрольного обмера; фото с рулеткой и привязкой к стене или углу	Вопроса в реестре нет: Альбом принимает положение стояков и радиаторов отопления без обмера. Результат принимает: Инженер ОВ
О-4	все помещения	Обмер	Контрольный обмер всех помещений: стороны, диагонали, проёмы, высота потолка.	исполнитель	±5 мм; диагонали — разница от 5 мм подписывается	обмерный и монтажный планы, развёртки, мебель на заказ Листы: л. 21 — Обмерный план л. 25 — План расстановки мебели	акт контрольного обмера	К-1 Результат принимает: Архитектор
О-5	Все помещения квартиры	Обмер	Высота потолка в каждом помещении в нескольких точках: центр, углы, у проёмов.	Архитектор	±5 мм	Вертикальные размеры альбома: развёртки, шкафы, плитка, объёмы работ. Листы: л. 2–5 — Общие данные	акт контрольного обмера	К-2 Результат принимает: Архитектор
О-6	санузел, ванная, кухня	Обмер	Положение и сечение вентканалов (вентблока), тяга.	исполнитель	±10 мм	план вентиляции, потолки, короба Листы: л. 37 — План вентиляции	акт контрольного обмера	К-7 Результат принимает: Инженер ОВ
О-7	санузел (пом. 6), коридор	Обмер	Проём санузла в чистоте (ширина, высота) и откос от угла коридора; материал и толщина стены.	исполнитель	±5 мм	ведомость заполнения проёмов, план дверей Листы: л. 23 — План дверей и ведомость заполнения проёмов	акт контрольного обмера	К-8 Результат принимает: Архитектор
О-8	По месту	Обмер	Подтвердить на объекте принятое: подрайон климата не задан — принят не северный (жилые от 2,5 м)	Архитектор	±5 мм	Листы, где используется принятая величина. Листы: л. 2–5 — Общие данные	акт контрольного обмера	К-9 Результат принимает: Архитектор

Допущения и предложения на листе

Основа листа: размеры сняты с растрового плана заказчика без размеров: масштаб восстановлен по площадям помещений (≈ 11,8 мм на пиксель), контрольный обмер не выполнен (К-1); высота потолка 2700 мм принята: на плане заказчика её нет (К-2); толщины стен 300 / 120 мм приняты по плану заказчика, не замерены (К-1); разрешённая мощность 15 кВт принята по типовым ТУ для квартиры, ТУ заказчиком не переданы (К-4); подрайон климата не задан — принят не северный (жилые от 2,5 м) (К-9).

См. лист открытых вопросов (лист 6, записи К-1, К-2, К-4; лист 7, запись К-9).

Изм.	Кол.уч	Лист	№ док.	Подп.	Дата
Разраб.		Кырлан А.С.			14.11.26
Пров.					
ГИП					
Н. контр.					
Утв.					

ГД-2026-007-АИ

Квартира 65 м²

Общая площадь 65,24* м² · * размеры со скана, не замерены (реестр — л. 6–8, К-1)

Дизайн-проект интерьера

Стадия	Лист	Листов
РП	10	117

Задание на контрольный обмер и обследование.
Лист 2 из 3
М б/м

Кырлан Александр Сергеевич

выпуск 14.11.2026 № 9cc0b98f36 · стр. 10 из 139

Задание на контрольный обмер и обследование. Лист 3 из 3

ПРЕДВАРИТЕЛЬНО · не для производства работ · открыто пунктов: 14 (реестр — л. 6–8)

Что замерить, вскрыть и получить до заказа материалов и изделий

Этап 2. После демонтажа, до черновых работ

№	Где	Способ	Что сделать	Кто выполняет	Точность	Что пересчитается в альбоме	Чем подтверждается	Закрывает вопросы реестра
О-9	Гардеробная (пом. 1), Спальня (пом. 2), Кухня-гостиная (пом. 3), Прихожая (пом. 4), Коридор (пом. 5), Санузел (пом. 6), Ванная (пом. 7), Кладовая (пом. 8), Детская (пом. 9)	Обмер	Нивелировка плиты перекрытия и существующего пола после демонтажа покрытий: отметки в углах и по сетке, перепады по помещению, уклоны, отметки порогов (чистый пол в мокрых зонах принят -15 мм, 0 мм). Принятая толщина стяжки 33 мм, 50 мм и отметка чистого пола — расчётные, не от замера плиты.	Архитектор	±5 мм по отметке; ровность просвет под 2-метровой рейкой, горизонталь против 0,2 % длины помещения	Толщина стяжки и отметка чистого пола; уклоны к трапам и пороги; выпуски К1 относительно чистого пола (план разводки); объёмы стяжки и смеси в ВОР и спецификации. Листы: л. 52, 56 — План полов л. 40 — Схема разводки водопровода и канализации	акт контрольного обмера	Вопроса в реестре нет: Альбом принимает отметки плиты и толщину пирога пола без нивелировки. Результат принимает: Отделочник
О-10	Гардеробная (пом. 1), Спальня (пом. 2), Кухня-гостиная (пом. 3), Прихожая (пом. 4), Коридор (пом. 5), Санузел (пом. 6), Ванная (пом. 7), Кладовая (пом. 8), Детская (пом. 9)	Обмер	Вертикаль и плоскостность стен: отклонение от вертикали по высоте стены (отвес или лазерный уровень), просвет под правилом 2 м, кривизна углов. Нужно там, где от стены зависит изделие: облицовка плиткой (пом. 6, 7), штукатурка и окраска (пом. 1, 2, 3, 4, 5, 8, 9), встроенная мебель и кухня (пом. 3, 4, 9).	Архитектор	до 1 мм на 2 м (правило и клиновой щуп); вертикаль — мм на высоту стены, отклонения подписываются на плане	Толщина штукатурки и расход смеси в ВОР и спецификации; раскладка плитки (подрезка у стен); зазоры и крепление встроенной мебели и кухни. Листы: л. 52–55 — Раскладка плитки л. 57 — Ведомость отделки помещений	акт контрольного обмера	Вопроса в реестре нет: Альбом принимает стены ровными и вертикальными без замера. Результат принимает: Отделочник

Документы и данные закупки (не на объекте)

№	У кого, откуда	Способ	Что получить	К какому сроку	Что пересчитается в альбоме	Чем подтверждается	Закрывает вопросы реестра
О-11	Заказчик; организация, выдавшая технические условия	Документ	Технические условия на присоединение: разрешённая мощность.	До утверждения однолинейной схемы щита	Однолинейная схема щита: вводной аппарат и группы. Листы: л. 2–5 — Общие данные	копия документа	К-4 Результат принимает: Инженер-электрик
О-12	адрес объекта, СП 131.13330	Документ	Климатический подрайон по СП 131.13330 (по адресу объекта)	до заказа каркаса потолков	план потолков, разрезы, ведомость объёмов Листы: л. 49 — План потолков	копия документа	К-9 Результат принимает: Архитектор
О-13	все помещения	Документ	План БТИ, проект дома или техническое заключение: несущие стены, материал и толщина, серия дома.	до начала демонтажа и штробления	обмерный план, план демонтажа, трассы ЭОМ и ВК в штробах Листы: л. 21 — Обмерный план л. 22 — План демонтажа и монтажа перегородок	копия документа	К-10 Результат принимает: Архитектор

Примечания

1. Подтверждение: акт контрольного обмера (дата, кто присутствовал, прибор, перечень промеров с результатами, подписи присутствующих); к акту — фото вскрытий и узлов и техническое заключение организации, выполнившей обследование.
2. Номера листов — по ведомости рабочих чертежей комплекта (лист «Общие данные»).
3. Пункт исключается из задания при следующем выпуске, когда акт подписан, значение внесено в проект и листы перевыпущены; знак «*» у величины снимается только замером.

Допущения и предложения на листе

Основа листа: размеры сняты с растрового плана заказчика без размеров: масштаб восстановлен по площадям помещений (≈ 11,8 мм на пиксель), контрольный обмер не выполнен (К-1); высота потолка 2700 мм принята: на плане заказчика её нет (К-2); толщины стен 300 / 120 мм приняты по плану заказчика, не замерены (К-1); разрешённая мощность 15 кВт принята по типовым ТУ для квартиры, ТУ заказчиком не переданы (К-4); подрайон климата не задан — принят не северный (жилые от 2,5 м) (К-9).

См. лист открытых вопросов (лист 6, записи К-1, К-2, К-4; лист 7, запись К-9).

Изм.	Кол.уч	Лист	№ док.	Подп.	Дата
Разраб.		Кырлан А.С.			14.11.26
Пров.					
ГИП					
Н. контр.					
Утв.					

ГД-2026-007-АИ

Квартира 65 м²

Общая площадь 65,24* м² · * размеры со скана, не замерены (реестр — л. 6–8, К-1)

Дизайн-проект интерьера

Стадия	Лист	Листов
РП	11	117

Задание на контрольный обмер и обследование.
Лист 3 из 3
М б/м

Кырлан Александр Сергеевич

График закупок и работ. Лист 1 из 3

ПРЕДВАРИТЕЛЬНО · не для производства работ · открыто пунктов: 14 (реестр — л. 6–8)

Что заказывать и когда не раньше чего: относительный порядок без дат; срок поставки — из данных или «не задан» с записью реестра

Лист не содержит дат: контрольного обмера, подписанных решений автора и договоров ещё нет, и любая дата была бы выдумана. Вместо календаря — порядок и условия: замер → решение и выбор изделия → заказ → срок поставки → работа, которую позиция блокирует. Срок поставки печатается как срок, только если он задан в данных позиции. Нет — «срок поставки не задан» и ссылка на вопрос реестра о сроках; типовой диапазон практики стоит рядом как ориентир и заказывать по нему нельзя. Номера З-N и Р-N — строки этого листа, К-N — записи реестра открытых вопросов, О-N — позиции задания на контрольный обмер.

Закупки: что заказывается, от чего зависит заказ и какую работу блокирует

№	Позиция и где	1. Замер до заказа	2. Решение, выбор изделия, паспорт	3. Условие заказа	4. Срок поставки	5. Блокирует работу	Закрывает вопросы реестра
З-1	Двери скрытого монтажа с коробом под покраску в существующих проёмах: Д-3, Д-2, Д-5, Д-4 — 7 шт. пом. 1, 2, 3, 5	О-4: обмер: все помещения (К-1); до заказа мебели и дверей		После 1 и 2 и после получения срока у поставщика (вопроса о сроках нет); дата заказа — когда срок известен, не позднее чем за срок до начала Р-6.	срок поставки не задан (записи реестра нет) Ориентир практики (не срок поставщика): ≈ 30 дн.	Р-6 «штукатурка»: короб ставят до штукатурки (коробку ставят на черновой стадии; полотно навешивают после чистовой отделки стен)	К-1
З-2	Кухонный гарнитур по проекту кухни: модули М4, М5, М6, М7, М8, М9, М12, М13 пом. 3			После 1 и 2 и после получения срока у поставщика (вопроса о сроках нет); дата заказа — когда срок известен, не позднее чем за срок до начала Р-16.	срок поставки не задан (записи реестра нет) Ориентир практики (не срок поставщика): 4–8 нед. от замера	Р-16 «кухня и мебель»: замер кухни — по готовым стенам после штукатурки или плитки, до чистового пола; производство идёт параллельно со стяжкой и отделкой	
З-3	Встраиваемая техника кухни: М8 холодильник пом. 3			После 1 и 2 и после получения срока у поставщика (вопроса о сроках нет); дата заказа — когда срок известен, не позднее чем за срок до начала Р-16.	срок поставки не задан (записи реестра нет)	Р-16 «кухня и мебель»: паспорта и монтажные схемы — до изготовления модулей кухни: нишу и вентзазоры задаёт модель, а не типовая схема 60 см	
З-4	Стиральная машина: П22 (вертикальная загрузка 400 × 600 мм — условие закупки) пом. 7			После 1 и 2 и после получения срока у поставщика (вопроса о сроках нет); дата заказа — когда срок известен, не позднее чем за срок до начала Р-5.	срок поставки не задан (записи реестра нет)	Р-5 «черновая сантехника»: габарит и подводка — до закрытия люка и разводки	
З-5	Сантехнические приборы и инсталляции: П4, П20, П21, П1, П3 пом. 3, 6, 7	О-3: обмер: у окон		После 1 и 2 и после получения срока у поставщика (вопроса о сроках нет); дата заказа — когда срок известен, не позднее чем за срок до начала Р-5.	срок поставки не задан (записи реестра нет)	Р-5 «черновая сантехника»: инсталляцию ставят до обшивки ГКЛВ и до гидроизоляции стены	
З-6	Керамогранит и плитка: 2 поз. по артикулу и формату, 47,96 м² по раскладке пом. 4, 5, 6, 7	О-9: обмер: Гардеробная (пом. 1), Спальня (пом. 2), Кухня-гостиная (пом. 3), Прихожая (пом. 4), Коридор (пом. 5), Санузел (пом. 6), Ванная (пом. 7), Кладовая (пом. 8), Детская (пом. 9) О-10: обмер: Гардеробная (пом. 1), Спальня (пом. 2), Кухня-гостиная (пом. 3), Прихожая (пом. 4), Коридор (пом. 5), Санузел (пом. 6), Ванная (пом. 7), Кладовая (пом. 8), Детская (пом. 9)		После 1 и 2 и после получения срока у поставщика (вопроса о сроках нет); дата заказа — когда срок известен, не позднее чем за срок до начала Р-10.	срок поставки не задан (записи реестра нет)	Р-10 «плитка»: калибр партии измеряют до раскладки, раскладку пересчитывают до заказа	

Допущения и предложения на листе

Основа листа: размеры сняты с растрового плана заказчика без размеров: масштаб восстановлен по площадям помещений (≈ 11,8 мм на пиксель), контрольный обмер не выполнен (К-1); высота потолка 2700 мм принята: на плане заказчика её нет (К-2); толщины стен 300 / 120 мм приняты по плану заказчика, не замерены (К-1); разрешённая мощность 15 кВт принята по типовым ТУ для квартиры, ТУ заказчиком не переданы (К-4); подрайон климата не задан — принят не северный (жилые от 2,5 м) (К-9).
См. лист открытых вопросов (лист 6, записи К-1, К-2, К-4; лист 7, запись К-9).

						ГД-2026-007-АИ	
						Квартира 65 м²	
						Общая площадь 65,24* м² · * размеры со скана, не замерены (реестр — л. 6–8, К-1)	
Изм.	Кол.уч	Лист	№ док.	Подп.	Дата		
Разраб.		Кырлан А.С.			14.11.26	Дизайн-проект интерьера	Стадия: РП; Лист: 12; Листов: 117
Пров.							
ГИП							
Н. контр.						**График закупок и работ. Лист 1 из 3** М б/м	**Кырлан Александр Сергеевич**
Утв.							

выпуск 14.11.2026 № 9cc0b98f36 · стр. 12 из 139

График закупок и работ. Лист 2 из 3

Что заказывать и когда не раньше чего: относительный порядок без дат; срок поставки — из данных или «не задан» с записью реестра

Закупки: что заказывается, от чего зависит заказ и какую работу блокирует (продолжение)

№	Позиция и где	1. Замер до заказа	2. Решение, выбор изделия, паспорт	3. Условие заказа	4. Срок поставки	5. Блокирует работу	Закрывает вопросы реестра
З-7	Покрытие пола (доска) и плинтус: пом. 1, 2, 3, 8, 9 пом. 1, 2, 3, 8, 9	О-9: обмер: Гардеробная (пом. 1), Спальня (пом. 2), Кухня-гостиная (пом. 3), Прихожая (пом. 4), Коридор (пом. 5), Санузел (пом. 6), Ванная (пом. 7), Кладовая (пом. 8), Детская (пом. 9)		После 1 и 2 и после получения срока у поставщика (вопроса о сроках нет); дата заказа — когда срок известен, не позднее чем за срок до начала Р-13.	срок поставки не задан (записи реестра нет)	Р-13 «чистовые полы»: артикул и партия — до заказа; доску привозят к чистовым полам	
З-8	Встроенная мебель по замеру цеха: М11, С5 пом. 4, 9	О-4: обмер: все помещения (К-1); до заказа мебели и дверей		После 1 и 2 и после получения срока у поставщика (вопроса о сроках нет); дата заказа — когда срок известен, не позднее чем за срок до начала Р-16.	срок поставки не задан (записи реестра нет) Ориентир практики (не срок поставщика): 4–8 нед. от замера	Р-16 «кухня и мебель»: цех замеряет по готовым стенам; производство 4–8 недель идёт параллельно с отделкой	К-1

Работы: порядок и что не даёт начать

№	Работа (стадия технологической последовательности)	После	Что должно быть к началу: условия и закупки	Не начинать, пока открыто в реестре
Р-1	Демонтаж покрытий, отделки стен и потолков, дверных блоков и приборов; конструкции, стены и перегородки не трогать до технического заключения (стадия 1)		до начала: запрошены документы на дом и БТИ; контрольный обмер до демонтажа (что видно) сделан	
Р-2	Контрольный обмер на голых стенах и обследование (задание — лист «Задание на контрольный обмер») (стадия 2)	Р-1	после снятия отделки: видны стояки, каналы, щиток, толщины стен; до заказа всего, что делают по размеру	
Р-3	Перегородки и фальш-стены ГКЛ: разметка, каркас, обшивка (стадия 3)	Р-2	до начала: решение по нише санузла 2 принято автором; разметка по плану монтажа подписана; коробка скрытой двери — в каркас до обшивки	К-1: Размеры квартиры сняты с растрового плана заказчика без размерных цепочек: масштаб восстановлен по подписанным площадям помещений.
Р-4	Черновая электрика: штробы, короба, гофра, подрозетники, щит (стадия 4)	Р-2, Р-3	до начала: план электрики с высотами утверждён; штробы в стенах — только после технического заключения; мебель расставлена	К-4: Разрешённая мощность квартиры по ТУ неизвестна, принята 15 кВт.
Р-5	Черновая сантехника и вентиляция: разводка, выводы, инсталляции, короба стояков (стадия 5)	Р-2, Р-3	до начала: положение стояков замерено; модели инсталляций и машины выбраны (габариты рамы, подводка); инсталляцию ставят до обшивки ГКЛВ и до гидроизоляции Закупки к началу: З-4 (стиральная машина), З-5 (сантехника)	
Р-6	Коробки скрытых дверей, затем штукатурка стен и откосов (стадия 6)	Р-3, Р-4, Р-5	до начала: электрика и сантехника смонтированы, штробы заделаны; коробки скрытых дверей установлены до штукатурки (поэтому заказ дверей — раньше работы) Закупки к началу: З-1 (двери скрытого монтажа)	К-1: Размеры квартиры сняты с растрового плана заказчика без размерных цепочек: масштаб восстановлен по подписанным площадям помещений.
Р-7	Стяжка пола и тёплый пол (стадия 7)	Р-6	до начала: штукатурка сделана; трубы под стяжкой приняты; нивелировка плиты выполнена	

Допущения и предложения на листе

Основа листа: размеры сняты с растрового плана заказчика без размеров: масштаб восстановлен по площадям помещений (≈ 11,8 мм на пиксель), контрольный обмер не выполнен (К-1); высота потолка 2700 мм принята: на плане заказчика её нет (К-2); толщины стен 300 / 120 мм приняты по плану заказчика, не замерены (К-1); разрешённая мощность 15 кВт принята по типовым ТУ для квартиры, ТУ заказчиком не переданы (К-4); подрайон климата не задан — принят не северный (жилые от 2,5 м) (К-9).

См. лист открытых вопросов (лист 6, записи К-1, К-2, К-4; лист 7, запись К-9).

Изм.	Кол.уч	Лист	№ док.	Подп.	Дата
Разраб.		Кырлан А.С.			14.11.26
Пров.					
ГИП					
Н. контр.					
Утв.					

ГД-2026-007-АИ

Квартира 65 м²

Общая площадь 65,24* м² · * размеры со скана, не замерены (реестр — л. 6–8, К-1)

Дизайн-проект интерьера

Стадия	Лист	Листов
РП	13	117

График закупок и работ. Лист 2 из 3

М б/м

Кырлан Александр Сергеевич

выпуск 14.11.2026 № 9cc0b98f36 · стр. 13 из 139

График закупок и работ. Лист 3 из 3

ПРЕДВАРИТЕЛЬНО · не для производства работ · открыто пунктов: 14 (реестр — л. 6–8)

Что заказывать и когда не раньше чего: относительный порядок без дат; срок поставки — из данных или «не задан» с записью реестра

Работы: порядок и что не даёт начать (продолжение)

№	Работа (стадия технологической последовательности)	После	Что должно быть к началу: условия и закупки	Не начинать, пока открыто в реестре
Р-8	Гидроизоляция санузлов и тест проливом (стадия 8)	Р-7	до начала: стяжка набрала прочность и сухая по инструкции гидроизоляции; выводы стоят на проектных отметках	
Р-9	ГКЛ: короба инсталляции и стояков, ниши, потолки (стадия 9)	Р-4, Р-5	до начала: черновые сети в зоне коробов приняты; закладные под тяжёлое и карнизы стоят; светильники выбраны (вырезы)	
Р-10	Плитка и керамогранит: стены, затем пол; фартук (стадия 10)	Р-7, Р-8, Р-9	до начала: гидроизоляция принята; плитка выбрана, калибр партии измерен, раскладка пересчитана и подписана Закупки к началу: З-6 (плитка)	
Р-11	Шпаклёвка стен и потолков под окраску (стадия 11)	Р-6, Р-9, Р-10	до начала: плитка готова (грязные работы закончены); штукатурка и ГКЛ сухие	
Р-12	Окраска стен, потолков, откосов (стадия 13)	Р-11	до начала: шпаклёвка отшлифована и огрунтована; выкрасы утверждены, колеровка одной партией	
Р-13	Чистовые полы: инженерная доска (стадия 14)	Р-10, Р-12	до начала: влажность основания в норме, мокрые работы закончены; доска выбрана и привезена Закупки к началу: З-7 (доска и плинтус)	
Р-14	Полотна межкомнатных дверей, плинтусы, пороги (стадия 15)	Р-12, Р-13	до начала: чистовой пол уложен; полотна скрытых дверей — после чистовой отделки стен	
Р-15	Чистовая электрика и сантехника: механизмы, светильники, смесители, приборы (стадия 16)	Р-12, Р-14	до начала: отделка готова; механизмы, светильники и приборы выбраны и привезены	
Р-16	Кухня, встроенная и корпусная мебель, бытовая техника (стадия 17)	Р-14, Р-15	до начала: чистовая сантехника и электрика подведены к местам мебели; замер кухни снят по готовым стенам (после штукатурки или плитки, до чистового пола) Закупки к началу: З-2 (кухонный гарнитур), З-3 (техника кухни), З-8 (мебель по замеру)	К-1: Размеры квартиры сняты с растрового плана заказчика без размерных цепочек: масштаб восстановлен по подписанным площадям помещений.
Р-17	Сдача: осмотр по чек-листу, дефектная ведомость, устранение замечаний (стадия 18)	Р-15, Р-16	до начала: всё смонтировано; акты скрытых работ подписаны	

Примечания

1. Порядок работ — стадии технологической последовательности из 17 позиций, присутствующих в этом проекте (по строкам ведомости объёмов); остальные стадии таблицы knowledge/remont-tehnologiya.md в проекте не встречаются. Длительности работ не печатаются: их нет ни в данных, ни в нормах для этого объекта.
2. Типовые сроки — ориентир практики, не срок поставщика: скрытые двери — короб около 10 дн., полотно под покраску до 3 нед., шпон 4–5 нед., в среднем около 30 дн. (knowledge/workers/foreman.md, п. 2.4 (profil-doors)); кухня и корпусная мебель — 4–8 недель от замера (knowledge/remont-tehnologiya.md, разд. 2; knowledge/workers/foreman.md, п. 2.4). Заказ по ориентиру не назначается: срок получают у поставщика (вопрос реестра), после чего заказ планируют «не позднее чем за срок до начала работы».
3. Условия заказа берутся из реестра открытых вопросов и задания на контрольный обмер: позиция заказывается, когда закрыты замер (графа 1) и решение (графа 2). Закрывать их может только факт или решение автора с подписью; снять строку с листа можно только закрыв запись реестра.
4. Заказ по размеру до контрольного обмера не делают: двери, кухня и встроенная мебель зависят от обмера (К-11, К-13); скрытые двери, кроме того, зависят от решения по нише санузла 2 (проём Д-5 в перегородке П-1).
5. Номера листов — по ведомости рабочих чертежей комплекта (лист «Общие данные»).

Допущения и предложения на листе

Основа листа: размеры сняты с растрового плана заказчика без размеров: масштаб восстановлен по площадям помещений (≈ 11,8 мм на пиксель), контрольный обмер не выполнен (К-1); высота потолка 2700 мм принята: на плане заказчика её нет (К-2); толщины стен 300 / 120 мм приняты по плану заказчика, не замерены (К-1); разрешённая мощность 15 кВт принята по типовым ТУ для квартиры, ТУ заказчиком не переданы (К-4); подрайон климата не задан — принят не северный (жилые от 2,5 м) (К-9).
См. лист открытых вопросов (лист 6, записи К-1, К-2, К-4; лист 7, запись К-9).

Изм.	Кол.уч	Лист	№ док.	Подп.	Дата
Разраб.		Кырлан А.С.			14.11.26
Пров.					
ГИП					
Н. контр.					
Утв.					

ГД-2026-007-АИ

Квартира 65 м²

Общая площадь 65,24* м² · * размеры со скана, не замерены (реестр — л. 6–8, К-1)

Дизайн-проект интерьера

Стадия	Лист	Листов
РП	14	117

График закупок и работ. Лист 3 из 3

М б/м


Кырлан Александр Сергеевич

Календарный график работ и закупок

ПРЕДВАРИТЕЛЬНО · не для производства работ · открыто пунктов: 14 (реестр — л. 6–8)

Недели, зависимости, техпаузы и даты заказа длинных позиций · длительности — ориентир по таблице типовых сроков, не обещание бригады

№	Работа	Нед.	После
Р-1	**демонтаж**	1	
Р-2	**контрольный обмер**	0,5	Р-1
Р-3	**перегородки ГКЛ**	0,75	Р-2
Р-4	**черновая электрика**	1,5	Р-3, Р-2
Р-5	черновая сантехника	1	Р-3, Р-2
Р-6	**штукатурка**	2,25	Р-4, Р-5, Р-3
Р-7	**стяжка**	0,75	Р-6
Р-8	**гидроизоляция**	0,5	Р-7
Р-9	ГКЛ	1,5	Р-4, Р-5
Р-10	**плитка**	3	Р-8, Р-9, Р-7
Р-11	**шпаклёвка**	2,5	Р-10, Р-9, Р-6
Р-12	**окраска**	2	Р-11
Р-13	**чистовые полы**	1	Р-12, Р-10
Р-14	**двери и плинтусы**	0,75	Р-13, Р-12
Р-15	**чистовая электрика и сантехника**	1	Р-14, Р-12
Р-16	**кухня и мебель**	1	Р-15, Р-14
Р-17	**сдача**	0,75	Р-16, Р-15
Закупки: заказать не позднее — «◆»; от заказа до поставки — штриховая полоса; срок поставки — только из данных или «ориентир практики»			
З-1	Двери скрытого монтажа с коробом под покраску в существующих проёмах: Д-3, Д-2, Д-5, Д-4	4,25	для Р-6
З-2	Кухонный гарнитур по проекту кухни: модули М4, М5, М6, М7, М8, М9, М12, М13	6	для Р-16
З-3	Встраиваемая техника кухни: М8 холодильник		для Р-16
З-4	Стиральная машина: П22 (вертикальная загрузка 400 × 600 мм — условие закупки)		для Р-5
З-5	Сантехнические приборы и инсталляции: П4, П20, П21, П1, П3		для Р-5
З-6	Керамогранит и плитка: 2 поз. по артикулу и формату, 47,96 м² по раскладке		для Р-10
З-7	Покрытие пола (доска) и плинтус: пом. 1, 2, 3, 8, 9		для Р-13
З-8	Встроенная мебель по замеру цеха: М11, С5	6	для Р-16

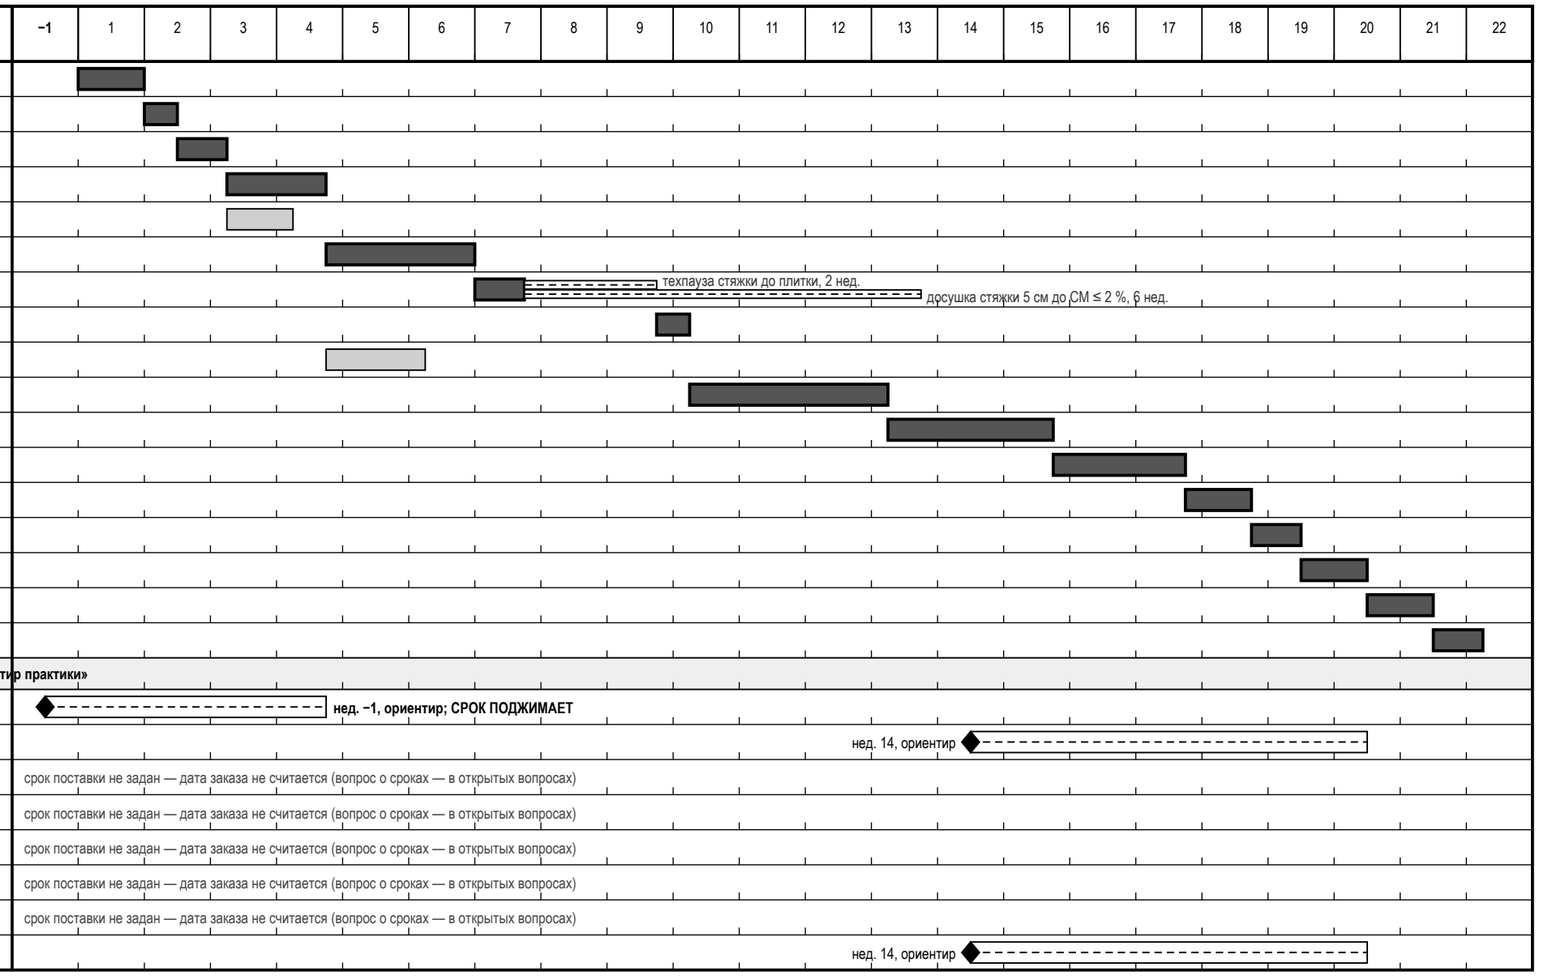

Итого: ≈ 21,25 нед. · жирная линия и тёмная полоса — критический путь

Примечания

1. Длительности этапов — типовые сроки по площади 65,24 м² (таблица «Свод для графика»: недели по этапам для 45, 80 и 120 м², середина вилки, линейная интерполяция); это ориентир, а не норма и не обещание бригады. Контрольный обмер — ориентир 0,5 нед. (в таблице нет).
2. Зависимости «после» — из графика закупок и работ (лист «График закупок и работ»); каждая работа начинается после конца предшественников. Техпаузы стоят отдельными полосами, а не спрятаны в длительности: стяжка → плитка — не менее 2 нед.; стяжка → чистовой пол — досушка стяжки 5 см до СМ ≤ 2 % — 6 нед. (ориентир «1 нед. на 1 см до 4 см, 5 см — 6 нед., 6 см — 8 нед.»; решает замер).
3. График последовательный и поэтому консервативный: в жизни шпаклёвка, плитка и досушка стяжки идут частично параллельно (таблица типовых сроков для 65,24 м²: 14–18 нед.). Совмещения — решение прораба после обмера.
4. Закупки: «заказать не позднее» = начало работы, которой нужна позиция, минус срок поставки. Срок поставки — из данных проекта (срок поставки позиции, срок изготовления обоев в отделке); если его нет, в графике стоит типовой диапазон практики с пометкой «ориентир» — это не срок поставщика, его надо получить до заказа. Кухню и встроенную мебель заказывают после замера по готовым стенам (после штукатурки). Позиции без срока дат заказа не имеют.
5. «Срок поджимает»: самая поздняя дата заказа раньше, чем позицию можно заказать (до замера или обмера): сдвиньте начало работ, ищите изделие с меньшим сроком или заказывайте по предварительному размеру — решение прораба и заказчика.

Допущения и предложения на листе

Основа листа: размеры сняты с растрового плана заказчика без размеров: масштаб восстановлен по площадям помещений (≈ 11,8 мм на пиксель), контрольный обмер не выполнен (К-1); высота потолка 2700 мм принята: на плане заказчика её нет (К-2); толщины стен 300 / 120 мм приняты по плану заказчика, не замерены (К-1); разрешённая мощность 15 кВт принята по типовым ТУ для квартиры, ТУ заказчиком не переданы (К-4); подрайон климата не задан — принят не северный (жилые от 2,5 м) (К-9).
См. лист открытых вопросов (лист 6, записи К-1, К-2, К-4; лист 7, запись К-9).

Изм.	Кол.уч	Лист	№ док.	Подп.	Дата
Разраб.		Кырлан А.С.			14.11.26
Пров.					
ГИП					
Н. контр.					
Утв.					

ГД-2026-007-АИ

Квартира 65 м²

Общая площадь 65,24* м² · * размеры со скана, не замерены (реестр — л. 6–8, К-1)

Дизайн-проект интерьера

Стадия	Лист	Листов
РП	15	117

Календарный график работ и закупок

М б/м

Кырлан Александр Сергеевич

выпуск 14.11.2026 № 9cc0b98f36 · стр. 15 из 139

Чек-лист приёмки по этапам. Лист 1 из 4

По этапам Р-1…Р-N: что проверить, чем, какой допуск и какой акт подписать до закрытия работы

ПРЕДВАРИТЕЛЬНО · не для производства работ · открыто пунктов: 14 (реестр — л. 6–8)

Приёмка по этапам: контрольные точки, допуски и акты скрытых работ

Этап	Контрольная точка (дальше не пускают без подписи)	Что проверяют	Чем	Допуск	Основание	Подпись	Акт скрытых работ / документ
Р-1	Демонтаж До начала демонтажа: запрошены документы на дом и БТИ	Что снимается и что не трогается: покрытия, отделка, дверные блоки; несущие стены и перегородки — без изменений	осмотр по плану демонтажа	снятое — только по плану; несущее не затрагивать	практика		Фото помещений до и после демонтажа; перечень снятого в журнале работ.
Р-2	Контрольный обмер Контрольный обмер на голых стенах сделан до заказа всего, что делают по размеру	Размеры помещений и проёмов, диагонали, положение стояков, щитка, каналов, толщины стен	рулетка, лазерный дальномер, уровень	допуск задаёт проект; расхождение с планом — в перечень открытых вопросов до заказа	практика		Протокол контрольного обмера с эскизом; расхождения занесены в открытые вопросы.
Р-3	Перегородки ГКЛ Перегородки: разметка против плана монтажа подписана до обшивки	Шаг саморезов: потолок 150 мм; стена 200 мм (лист вертикально) или 300 мм (горизонтально)	рулетка	150 / 200 / 300 мм	практика (СП 163.1325800.2014)		Акт скрытых работ: каркас ГКЛ, закладные под тяжёлое, звукоизоляция в перегородках — до обшивки (фото закладных с привязками); армирование и примыкание к несущим.
		Отступ самореза от кромки и угла листа; расстояние между саморезами на стыке листов	рулетка	5–10 мм от кромки; не менее 15 мм на стыке	практика (СП 163.1325800.2014)		
		Заделка стыков: лента и не менее 2 слоёв шпаклёвки; шляпки утоплены вровень, без прорыва картона	визуально, на просвет	без трещин после высыхания	практика		
		Прогиб каркаса: нет люфта между листом и профилем	простукивание, нажатие рукой	точной цифры нет — сверить перед актом	практика		
Р-4	Черновая электрика Черновая электрика: трассы, высоты подрозетников, замер изоляции подписаны до заделки	Сопротивление изоляции проводки (цепи до 1000 В)	мегаомметр	не менее 0,5 МОм	норматив (ПУЭ, гл. 1.8)		Акт скрытых работ на трассы проводки и слаботочные линии до закрытия штукатуркой и ГКЛ; исполнительная схема трасс с привязками; заземление и уравнивание потенциалов в санузле протокол и фото.
		Целостность и маркировка: PE жёлто-зелёный, N — синий, L — прочие цвета	визуально, прозвонка	каждый проводник промаркирован	практика		
		Высоты подрозетников и привязки — по плану розеток и выключателей	рулетка, уровень	по проекту; от чистого пола	практика		
Р-5	Черновая сантехника Черновая сантехника: опрессовка, отметки выводов, инсталляции подписаны до зашивки	Опрессовка водоснабжения: рабочее давление до 0,6 МПа — испытание 0,9 МПа; выше 0,6 МПа — по расчёту	опрессовочный насос, манометр	выдержка 10 мин (поквартирная); падение: пластик не более 0,06 МПа за 30 мин, сталь не более 0,05 МПа за 10 мин	практика (СП 73.13330)		Акт опрессовки (давление, время, результат); акт скрытых работ на трассы в стенах, полу и коробах; инсталляции, скрытые смесители, трапы — фото с рулеткой и отметками.
		Уклон канализации Ø40–50	уровень, построитель плоскостей	не менее 20 мм на 1 м	норматив (СП 30.13330)		
		Протечки в соединениях, сифоны, смесители, гибкая подводка	осмотр под давлением, салфетка на стыках	нет капель и влажных следов в контрольное время	практика		

Допущения и предложения на листе

Основа листа: размеры сняты с растрового плана заказчика без размеров: масштаб восстановлен по площадям помещений (≈ 11,8 мм на пиксель), контрольный обмер не выполнен (К-1); высота потолка 2700 мм принята: на плане заказчика её нет (К-2); толщины стен 300 / 120 мм приняты по плану заказчика, не замерены (К-1); разрешённая мощность 15 кВт принята по типовым ТУ для квартиры, ТУ заказчиком не переданы (К-4); подрайон климата не задан — принят не северный (жилые от 2,5 м) (К-9).

См. лист открытых вопросов (лист 6, записи К-1, К-2, К-4; лист 7, запись К-9).

Изм.	Кол.уч	Лист	№ док.	Подп.	Дата
Разраб.		Кырлан А.С.			14.11.26
Пров.					
ГИП					
Н. контр.					
Утв.					

ГД-2026-007-АИ

Квартира 65 м²

Общая площадь 65,24* м² · * размеры со скана, не замерены (реестр — л. 6–8, К-1)

Дизайн-проект интерьера

Стадия	Лист	Листов
РП	16	117

Чек-лист приёмки по этапам. Лист 1 из 4

М б/м

Кырлан Александр Сергеевич

выпуск 14.11.2026 № 9cc0b98f36 · стр. 16 из 139

Чек-лист приёмки по этапам. Лист 2 из 4

По этапам Р-1…Р-N: что проверить, чем, какой допуск и какой акт подписать до закрытия работы

Приёмка по этапам: контрольные точки, допуски и акты скрытых работ (продолжение)

Этап	Контрольная точка (дальше не пускают без подписи)	Что проверяют	Чем	Допуск	Основание	Подпись	Акт скрытых работ / документ
		Отметки выводов и положение инсталляций до зашивки и гидроизоляции	рулетка в кадре, фото	по листу выводов	практика		
Р-6	Штукатурка Маяки стен проверены до штукатурки; коробки скрытых дверей стоят до штукатурки	Отклонение от вертикали (простая / улучшенная / высококачественная штукатурка)	отвес, лазерный уровень	3 / 2 / 1 мм на 1 м; не более 15 / 10 / 5 мм на высоту	практика (СП 71.13330.2017)		Фото коробок скрытых дверей с отметкой чистого пола — до штукатурки; класс штукатурки (простая / улучшенная / высококачественная) назван в договоре.
		Отклонение от горизонтали	уровень, правило	3 / 2 / 1 мм на 1 м; не более 15 / 10 / 5 мм на длину	практика (СП 71.13330.2017)		
		Неровности (плоскостность)	правило 2 м и щуп	до 5 / 3 / 2 мм на 1 м; не более 3 / 2 / 2 неровностей на 4 м²	практика (СП 71.13330.2017)		
		Влажность основания перед шпаклёвкой и отделкой	влагомер	верхние 20–30 мм — не более 5 % по массе	норматив (СП 71, табл. 7.2)		
Р-7	Стяжка Стяжка: подготовка, после заливки ровность, затем замер СМ перед чистовым полом	Ровность: просвет под рейкой 2 м	рейка 2 м, клиновой щуп	под паркет, ламинат — 2 мм; под гидроизоляцию до 4 мм; прочие покрытия — до 6 мм (цифры расходятся между источниками — сверить перед актом)	практика (СП 29.13330)		Акт скрытых работ на стяжку (толщина, армирование) до чистового пола; протокол ровности и протокол СМ-влажности; звукоизоляция и демпферная лента под стяжкой — фото и паспорт; контуры тёплого пола до заливки — схема укладки и замер сопротивления.
		Отклонение от горизонтали по помещению	уровень, нивелир	не более 0,2 % длины помещения	практика (СП 29.13330)		
		Число точек измерения	рейка	не менее 3 на 30 м² или 1 на небольшое помещение	практика		
		Отслоения и пустоты	простукивание молотком или киянкой	глухой звук — зона вскрывается и переделывается	практика		
		Влажность перед укладкой доски: цементная стяжка	влагомер; СМ-замер	ЦПС не более 2,0 % СМ (с тёплым полом не более 1,8 %); влагомер для плитки — не более 5 %	практика (СП 71; рекомендации производителей)		
Р-8	Гидроизоляция Гидроизоляция: пролив 24 ч подпись до плитки	Заведение на стены не ниже 200 мм от чистого пола; за ванной — 300 мм выше борта; в душе без поддона — на высоту лейки	рулетка	не менее 200 мм	норматив (СП 71.13330.2017, п. 8.6.5); остальное — практика		Акт теста проливом, фото узлов и высоты заведения на стены — до плитки.
		Тест проливом: слой воды 10–30 мм, контроль уровня и потолка соседа снизу	линейка, визуально	24 ч (минимум 12 ч); падения уровня и протечки нет	практика		
		Два слоя обмазки с межслойной сушкой, лента в углах и манжеты на выводах	визуально	по инструкции производителя	практика		
Р-9	ГКЛ Короба, ниши и потолки: черновые сети в зоне коробов приняты до обшивки	Шаг саморезов, отступ от кромки, заделка стыков (как у перегородок)	рулетка, визуально	потолок 150 мм; кромка 5–10 мм; стык — лента и 2 слоя шпаклёвки	практика (СП 163.1325800.2014)		Акт скрытых работ: каркас ГКЛ, закладные, звукоизоляция — фото до обшивки; воздуховоды в коробах и за потолком — фото и схема.

Допущения и предложения на листе

Основа листа: размеры сняты с растрового плана заказчика без размеров: масштаб восстановлен по площадям помещений (≈ 11,8 мм на пиксель), контрольный обмер не выполнен (К-1); высота потолка 2700 мм принята: на плане заказчика её нет (К-2); толщины стен 300 / 120 мм приняты по плану заказчика, не замерены (К-1); разрешённая мощность 15 кВт принята по типовым ТУ для квартиры, ТУ заказчиком не переданы (К-4); подрайон климата не задан — принят не северный (жилые от 2,5 м) (К-9).

См. лист открытых вопросов (лист 6, записи К-1, К-2, К-4; лист 7, запись К-9).

Изм.	Кол.уч	Лист	№ док.	Подп.	Дата
Разраб.		Кырлан А.С.			14.11.26
Пров.					
ГИП					
Н. контр.					
Утв.					

ГД-2026-007-АИ

Квартира 65 м²

Общая площадь 65,24* м² · * размеры со скана, не замерены (реестр — л. 6–8, К-1)

Дизайн-проект интерьера	Стадия	Лист	Листов
	РП	17	117

Чек-лист приёмки по этапам. Лист 2 из 4

М б/м

Кырлан Александр Сергеевич

выпуск 14.11.2026 № 9cc0b98f36 · стр. 17 из 139

Чек-лист приёмки по этапам. Лист 3 из 4

По этапам Р-1…Р-N: что проверить, чем, какой допуск и какой акт подписать до закрытия работы

Приёмка по этапам: контрольные точки, допуски и акты скрытых работ (продолжение)

Этап	Контрольная точка (дальше не пускают без подписи)	Что проверяют	Чем	Допуск	Основание	Подпись	Акт скрытых работ / документ
		Закладные под тяжёлое, карнизы, подвесные светильники на месте до обшивки	фото с привязками	по плану потолков и узлам	практика		
		Ревизионные люки: доступ к арматуре и ревизиям сохранён	осмотр	по листу ВК	практика		
Р-10	Плитка Раскладка плитки: первая плита и первый ряд проверены по развёртке; плитка выбрана, калибр партии измерен	Уступы между смежными плитками	линейка, на просвет	не более 1 мм	норматив (СП 71.13330.2017)		Раскладка подписана до начала плитки; протокол первого ряда; акт теста проливом приложен (этап гидроизоляции).
		Ширина шва и его прямолинейность	линейка, калибр	до 6 мм ручная укладка; фактическая по проекту ±0,5 мм	практика		
		Отклонение рядов от вертикали и горизонтали	уровень, правило, отвес	1,5 мм на 1 м длины	практика		
		Ровность облицовки	правило 2 м и щуп	не более 2–4 мм (цифра расходится по источникам)	практика		
		Пустоты под плиткой	простукивание всей площади	до 10 % площади допустимо; свыше 25 % под одной плиткой — брак	практика		
Р-11	Шпаклёвка Шпаклёвка Q3/Q4: проверка боковым светом до окраски	Класс основания под окраску: Q3 — сплошное финишное шпаклевание; Q4 — под направленный свет	переносной прожектор у поверхности под острым углом	Q3: царапины от абразива до 0,5 мм; Q4 — без видимых царапин и теней; неровность на 2 м: Q3 — 1 мм, Q4 — 0,5 мм	практика (Q-классы — не норматив СП, а согласованный критерий)		Класс (Q3 или Q4) назван в договоре; грунтование и армирование стыков перед шпаклёвкой — запись в журнале.
Р-12	Окраска Выкрасы утверждены, колеровка одной партией	Окраска без полос, подтёков, пропусков; цвет — по колерной карте	боковой свет, образец выкраса	без видимых дефектов при боковом свете	практика		Утверждённые выкрасы; остаток колеровки одной партии — для подкраски.
		Основание сухое, огрунтованное; защита от прямого солнца при высыхании	осмотр	по ТУ краски	норматив (СП 71.13330.2017, п. 7.5.2)		
Р-13	Чистовые полы Чистовые полы: влажность, ровность, уступы, зазоры — до укладки доски; мокрые работы закончены	Деформационный зазор у стен и порогов (доска, ламинат)	линейка, клинья при укладке	8–15 мм (чаще 10 мм); у ламината 5–10 мм по СП 71	практика (требования производителей); норматив (СП 71, п. 8.10.14)		Протокол СМ-влажности стяжки до укладки; паспорт и партия доски.
		Перепад основания под покрытие	правило 2 м и щуп	не более 2 мм на 2 м	практика		
		Зазоры и перепады между досками; скрип; видимый зазор в замке — брак	щуп, рука, шаг	«ступеньки» нет	практика		
		Влажность помещения при укладке и после	гигрометр	не более 60 %, без сквозняков	норматив (СП 71, п. 8.1.7)		

Допущения и предложения на листе

Основа листа: размеры сняты с растрового плана заказчика без размеров: масштаб восстановлен по площадям помещений (≈ 11,8 мм на пиксель), контрольный обмер не выполнен (К-1); высота потолка 2700 мм принята: на плане заказчика её нет (К-2); толщины стен 300 / 120 мм приняты по плану заказчика, не замерены (К-1); разрешённая мощность 15 кВт принята по типовым ТУ для квартиры, ТУ заказчиком не переданы (К-4); подрайон климата не задан — принят не северный (жилые от 2,5 м) (К-9).

См. лист открытых вопросов (лист 6, записи К-1, К-2, К-4; лист 7, запись К-9).

Изм.	Кол.уч	Лист	№ док.	Подп.	Дата
Разраб.		Кырлан А.С.			14.11.26
Пров.					
ГИП					
Н. контр.					
Утв.					

ГД-2026-007-АИ

Квартира 65 м²

Общая площадь 65,24* м² · * размеры со скана, не замерены (реестр — л. 6–8, К-1)

Дизайн-проект интерьера

Стадия	Лист	Листов
РП	18	117

Чек-лист приёмки по этапам. Лист 3 из 4

М б/м

Кырлан Александр Сергеевич

выпуск 14.11.2026 № 9cc0b98f36 · стр. 18 из 139

Чек-лист приёмки по этапам. Лист 4 из 4

По этапам Р-1…Р-N: что проверить, чем, какой допуск и какой акт подписать до закрытия работы

Приёмка по этапам: контрольные точки, допуски и акты скрытых работ (продолжение)

Этап	Контрольная точка (дальше не пускают без подписи)	Что проверяют	Чем	Допуск	Основание	Подпись	Акт скрытых работ / документ
Р-14	Двери и плинтусы Полотна и плинтусы — после чистового пола; скрытые полотна после чистовой отделки стен	Отклонение коробки от вертикали	отвес, уровень	1,5 мм на 1 м, не более 3 мм на коробку	практика (ТР 105-00, пересказ)		Коробки скрытых дверей приняты до штукатурки (этап штукатурки); паспорт на полотна.
		Зазор между полотном и коробкой по периметру	щуп	2–4 мм по бокам и верху (единого норматива нет)	практика		
		Открывание и закрывание: без перекоса, плавный ход петель и доводчика	визуально, от руки	без задевания коробки и пола	практика		
Р-15	Чистовая электрика и сантехника Чистовая электрика и сантехника: протокол электролаборатории и проверка УЗО до подписи акта	УЗО: кнопка «Тест»; время отключения; ток отключения	кнопка на аппарате; прибор проверки УЗО (не мультиметр)	отключает; не более 0,3 с; 50–100 % от IΔn	практика измерений		Протокол измерений аккредитованной электролаборатории (изоляция по группам, УЗО, PE, фаза-ноль); исполнительная схема щита; акт опрессовки приложен (этап ВК).
		Сопротивление изоляции готовых линий; петля фаза-ноль для срабатывания автоматов	мегаомметр; прибор петли фаза-ноль	изоляция не менее 0,5 МОм; петля — по проекту	норматив (ПУЭ, гл. 1.8) / по проекту		
		Смесители, сифоны, гибкая подводка: пробный пуск воды	визуально под нагрузкой	нет подтёков в контрольное время	практика		
Р-16	Кухня и мебель Кухня и мебель: замер кухни снят по готовым стенам; чистовая электрика и сантехника подведены	Привязка выводов и розеток к модулям кухни; вытяжка, вентиляция	рулетка, сверка с листом кухни	по проекту кухни	практика		Акт передачи кухни; паспорта техники и гарантийные талоны.
		Тяга вентиляции у решёток	лист бумаги у решётки	бумага притягивается; при сомнениях — замер анемометром	практика		
Р-17	Сдача Финальная приёмка по таблицам СП 71: дефектная ведомость и акт	Стены, потолки, полы, плитка, двери, окна осмотр по чек-листу этапов выше	правило 2 м, уровень, щуп, боковой свет, влагомер	по таблицам выше	практика		Дефектная ведомость и акт приёмки; гарантия: по умолчанию претензии по качеству работ — 2 года, в договоре прописывается отдельно.
		Полный пакет документов: акты скрытых работ, протокол электролаборатории, акт опрессовки, исполнительные схемы, гарантийные обязательства	комплектность	пакет собран до подписи акта	практика		

Примечания

1. Метка основания: «норматив» — цифра подтверждена текстом СП, ГОСТ или ПУЭ; «практика» — отраслевая конвенция или один источник: к спору не годится без сверки первоисточника (СП 71.13330.2017, СП 29.13330, СП 163.1325800.2014, ПУЭ гл. 1.8, СП 73.13330, СП 30.13330).
2. Класс штукатурки (простая / улучшенная / высококачественная) и класс основания под окраску (Q3 или Q4) называются в договоре подряда: допуск выбирается по ним. Q-классы — не норматив, а согласованный сторонами критерий.
3. Акт скрытых работ подписывают до того, как работа закрыта следующим слоем (штукатуркой, плиткой, стяжкой, обшивкой): постфактум он слабее — осматривать нечего. Подписывают заказчик (или технадзор), подрядчик; при перепланировке — автор проекта. Каждую зону снимают до закрытия с рулеткой в кадре и привязкой к стене.
4. По умолчанию, если срок не прописан в договоре, претензии по качеству работ можно предъявить в течение 2 лет со дня приёмки; в договоре гарантийный срок и сроки на скрытые работы рекомендуется назвать явно.

Допущения и предложения на листе

Основа листа: размеры сняты с растрового плана заказчика без размеров: масштаб восстановлен по площадям помещений (≈ 11,8 мм на пиксель), контрольный обмер не выполнен (К-1); высота потолка 2700 мм принята: на плане заказчика её нет (К-2); толщины стен 300 / 120 мм приняты по плану заказчика, не замерены (К-1); разрешённая мощность 15 кВт принята по типовым ТУ для квартиры, ТУ заказчиком не переданы (К-4); подрайон климата не задан — принят не северный (жилые от 2,5 м) (К-9).

См. лист открытых вопросов (лист 6, записи К-1, К-2, К-4; лист 7, запись К-9).

						ГД-2026-007-АИ	
						Квартира 65 м²	
						Общая площадь 65,24* м² · * размеры со скана, не замерены (реестр — л. 6–8, К-1)	
Изм.	Кол.уч	Лист	№ док.	Подп.	Дата	Дизайн-проект интерьера	Стадия: РП; Лист: 19; Листов: 117
Разраб.		Кырлан А.С.			14.11.26		
Пров.							
ГИП							
						Чек-лист приёмки по этапам. Лист 4 из 4	Кырлан Александр Сергеевич
Н. контр.						М б/м	
Утв.							

выпуск 14.11.2026 № 9cc0b98f36 · стр. 19 из 139

Лист → мастер

Мастер → листы альбома и документы, которые ему нужны

ПРЕДВАРИТЕЛЬНО · не для производства работ · открыто пунктов: 14 (реестр — л. 6–8)

Какому мастеру какие листы (номера — как в штампе)

Мастер	Что делает по альбому	Листы	Кроме чертежей — документы	Листов
Замерщик и прораб (до начала работ)	Контрольный обмер на голых стенах, сверка размеров и диагоналей, ответы на открытые вопросы до заказа	2–11, 21	Задание на контрольный обмер; лист открытых вопросов	11
Гипсокартонщик и монтажник перегородок	Демонтаж и возведение перегородок, каркас, короба инсталляции, ниши, потолки; закладные под навесное	22, 49–51, 74, 76	Ведомость материалов каркаса; акт скрытых работ на каркас	6
Электрик	Группы щита, подрозетники и высоты, трассы, свет, управление светом, слаботочка, тёплый пол	29–36, 48, 80–102	Таблица нагрузок; ведомость изделий; протокол электролаборатории	32
Сантехник	Выводы воды и канализации, разводка, аксонометрии, инсталляции, короба стояков	39–47, 80–102	Спецификация ВК; акт опрессовки; акт пролива	32
Монтажник вентиляции, отопления и кондиционеров	Вентиляция, радиаторы и тёплые полы, кондиционеры: места, размеры, трассы и дренаж	37–38	Акт опрессовки азотом (кондиционеры); фото воздуховодов до закрытия	2
Штукатур, шпаклёвщик, маляр, паркетчик	Основание стен, окраска и обои по колерной карте, полы и пороги, плинтус, узлы стыков	56–60, 80–103	Колерная карта и выкрасы; спецификация отделочных материалов	29
Плиточник	Раскладка и подрезка плитки стен, пола и фартука, гидроизоляция, швы, выводы в плитке	44–46, 52–55, 80–103	Ведомость плитки; акт теста проливом	31
Монтажник дверей и окон	Заполнение проёмов: размеры коробок, открывание, пороги, скрытые двери	23	Ведомость проёмов; паспорта на полотна	1
Мебельщик, кухонный монтажник	Кухня и мебель на заказ: габариты, членение, фурнитура, связка с электрикой и сантехникой	25–28, 67–78	Ведомость изделий; замер кухни по готовым стенам	16
Заказчик и комплектатор	Что и когда покупать, сколько с запасом, во что это обойдётся; свет, декор и текстиль; визуализации как должно получиться	1, 12–15, 48, 61–62, 65–66, 104–117	Список покупок; смета; календарный график	24
Прораб и технадзор (приёмка)	Приёмка этапов, акты скрытых работ, дефектная ведомость	15–20	Чек-лист приёмки по этапам; календарный график	6

Примечания

1. Номера листов — как в основной надписи: основные подряд (1, 2, 3…), «Д» — детализация мебели, «С» — ведомости, спецификации, узлы и сметы, «П» — приложение единого комплекта. «12–18» — все листы с 12 по 18.
2. Лист может быть у нескольких мастеров: развёртка стены нужна электрику (высоты точек), сантехнику (выводы), отделочнику (материалы) и плиточнику (раскладка). Общие листы (обмер, список листов, перечень вопросов) прораб раздаёт всем.
3. Мастер работает по чертежам и берёт в руки то, что назначено ему здесь; закупки, смету и график ведёт заказчик с прорабом. Лист, которого нет в таблице ни у одного мастера, — вопрос прорабу: чей он.

Допущения и предложения на листе

Основа листа: размеры сняты с растрового плана заказчика без размеров: масштаб восстановлен по площадям помещений (≈ 11,8 мм на пиксель), контрольный обмер не выполнен (К-1); высота потолка 2700 мм принята: на плане заказчика её нет (К-2); толщины стен 300 / 120 мм приняты по плану заказчика, не замерены (К-1); разрешённая мощность 15 кВт принята по типовым ТУ для квартиры, ТУ заказчиком не переданы (К-4); подрайон климата не задан — принят не северный (жилые от 2,5 м) (К-9).

См. лист открытых вопросов (лист 6, записи К-1, К-2, К-4; лист 7, запись К-9).

Изм.	Кол.уч	Лист	№ док.	Подп.	Дата
Разраб.		Кырлан А.С.			14.11.26
Пров.					
ГИП					
Н. контр.					
Утв.					

ГД-2026-007-АИ

Квартира 65 м²

Общая площадь 65,24* м² · * размеры со скана, не замерены (реестр — л. 6–8, К-1)

Дизайн-проект интерьера

Стадия	Лист	Листов
РП	20	117

Лист → мастер

М б/м

Кырлан Александр Сергеевич

выпуск 14.11.2026 № 9cc0b98f36 · стр. 20 из 139

01

Архитектурные решения



Кырлан Александр Сергеевич

выпуск 14.11.2026 № 9cc0b98f36 · стр. 21 из 139

Обмерный план

Существующее положение · размеры в мм · отметки от чистого пола

ПРЕДВАРИТЕЛЬНО · не для производства работ · открыто пунктов: 14 (реестр — л. 6–8)


Отметки по высоте

±0,000	чистый пол пом. 1–5, 8, 9; отсчёт высот
−0,015	чистый пол пом. 6, 7, ниже на 15 мм
−0,064*	верх плиты — расчёт, не замер (задание на обмер)
сущ. пол	снимается до плиты; не замерен (задание на обмер)

Принято, не определено или спорно

полностью — листы 6–8

К-10 — Несущие стены не определены: плана БТИ, проекта дома и технического заключения в материалах объекта нет (данные проекта пуст, structure.bearingStatus = pending)

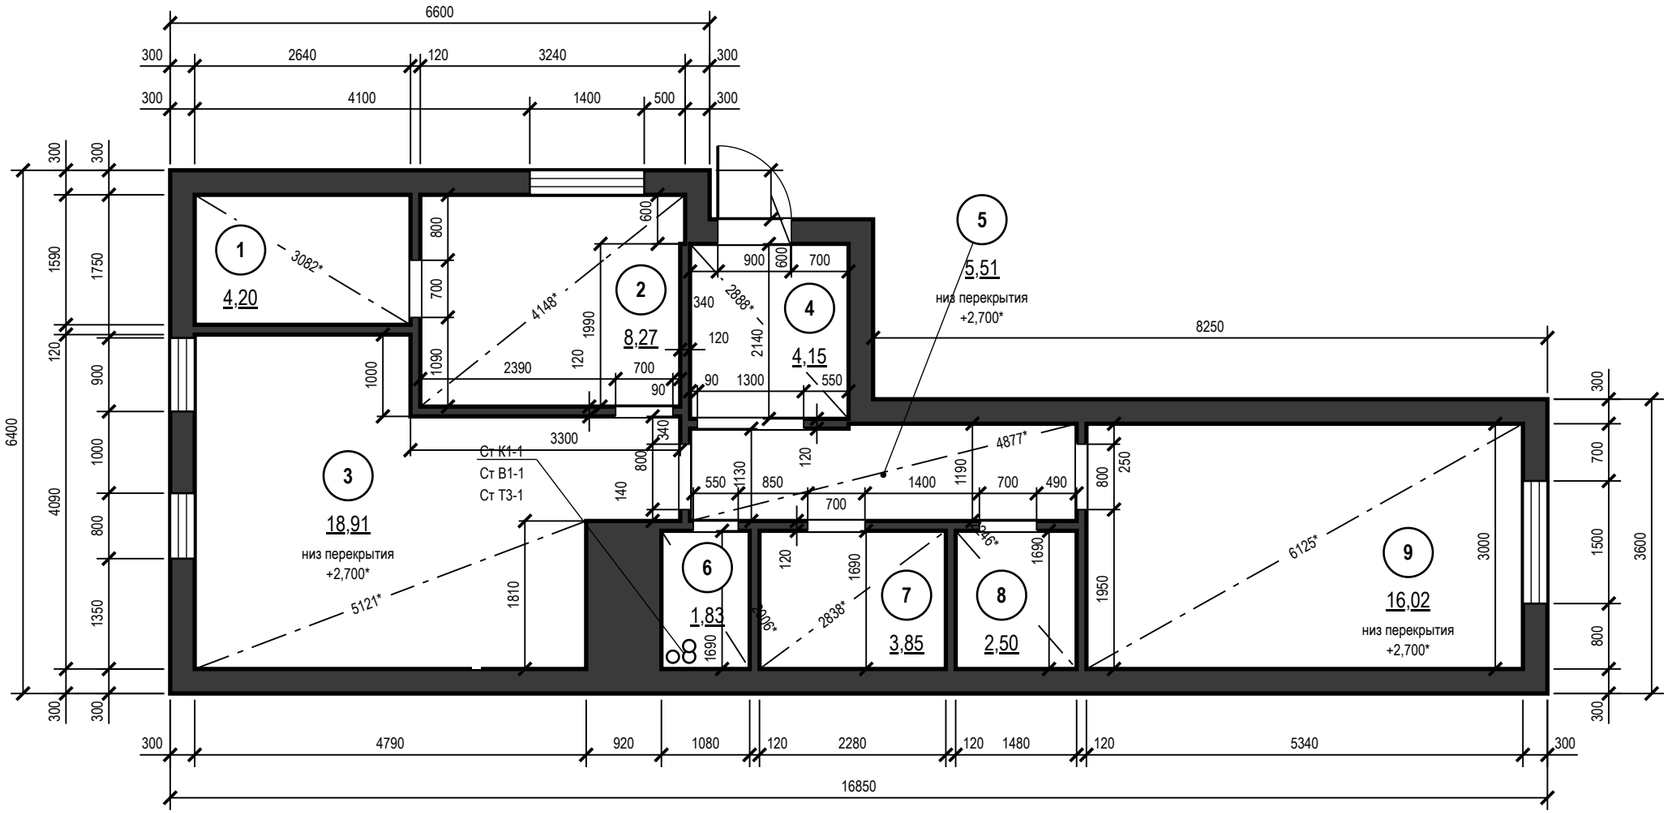

Экспликация помещений

№	Наименование	Площадь, м²
1	Гардеробная	4,20
2	Спальня	8,27
3	Кухня-гостиная	18,91
4	Прихожая	4,15
5	Коридор	5,51
6	Санузел	1,83
7	Ванная	3,85
8	Кладовая	2,50
9	Детская	16,02
	Итого (общая площадь)	**65,24**

Условные обозначения

- существующие стены (сечение)
- окно (рама, остекление)
- проём существующий, без заполнения (откосы)
- стояк: К1 — канализация, В1 — ХВС, Т3 — ГВС
- диагональ помещения — контроль прямоугольности
- (1) номер помещения, площадь м²

Примечания

1. Размеры — в мм по чистым поверхностям стен до отделки (по плану заказчика); площади — в м² по тем же размерам. До начала работ выполнить контрольный обмер.
2. Источник плана — допущение, не замер: растровый скан плана заказчика, размеры сняты с размерных цепочек, на объекте не замерены. Реестр: листы 6–8, вопрос К-1.
3. За отметку ±0,000 принят чистый пол, не существующий (блок отметок). «Низ перекрытия» у марки помещения — отметка низа перекрытия от ±0,000, как на развёртках и плане потолков (не высота потолка: потолок — по плану потолков); отметка со знаком «*» — принятая, не замер (вопрос К-2).
4. Толщины стен: наружные 300 мм, перегородки 120 мм; отличающиеся толщины и уступы размерами на плане.
5. Обмер — существующее положение: новых конструкций на листе нет, они — на плане монтажа.
6. Несущие стены не определены: до технического заключения все стены считать несущими; проёмы и штробы в них не выполнять.
7. Дверные проёмы показаны без заполнения (двери — лист 23); высота дверных проёмов 2100 мм, проёмов без двери 2100 мм; низ окон (подоконник) 800 мм от чистого пола, высота окон 1600 мм.
8. Диагонали — контрольные размеры; «*» — расчёт по принятому контуру (К-1), при обмере заменить замеренным; расхождение более 5 мм подписать на плане как перекос.
9. Размеры проверить на месте до начала работ; расхождение контрольных промеров ≤ 2 %.
10. Размеры короче 1 мм на листе цепочкой не показаны (две выносные линии на таком расстоянии сливаются): пом. 5, стена В — 40 мм от угла до проёма.

Допущения и предложения на листе

Основа листа: размеры сняты с растрового плана заказчика без размеров: масштаб восстановлен по площадям помещений (≈ 11,8 мм на пиксель), контрольный обмер не выполнен (К-1); высота потолка 2700 мм принята: на плане заказчика её нет (К-2); толщины стен 300 / 120 мм приняты по плану заказчика, не замерены (К-1); разрешённая мощность 15 кВт принята по типовым ТУ для квартиры, ТУ заказчиком не переданы (К-4); подрайон климата не задан — принят не северный (жилые от 2,5 м) (К-9).

Открытые вопросы и конфликты по листу: К-1, К-2, К-10.

См. лист открытых вопросов (лист 6, записи К-1, К-2, К-4; лист 7, записи К-9, К-10).

1000 мм · печать 1:1

Изм.	Кол.уч	Лист	№ док.	Подп.	Дата
Разраб.		Кырлан А.С.			14.11.26
Пров.					
ГИП					
Н. контр.					
Утв.					

ГД-2026-007-АИ

Квартира 65 м²

Общая площадь 65,24* м² · * размеры со скана, не замерены (реестр — л. 6–8, К-1)

Дизайн-проект интерьера

Стадия	Лист	Листов
РП	21	117

Обмерный план

М 1:75


Кырлан Александр Сергеевич

выпуск 14.11.2026 № 9cc0b98f36 · стр. 22 из 139

План демонтажа и монтажа перегородок

Существующее — серым, демонтаж — красным, монтаж — синим · размеры в мм

ПРЕДВАРИТЕЛЬНО · не для производства работ · открыто пунктов: 14 (реестр — л. 6–8)

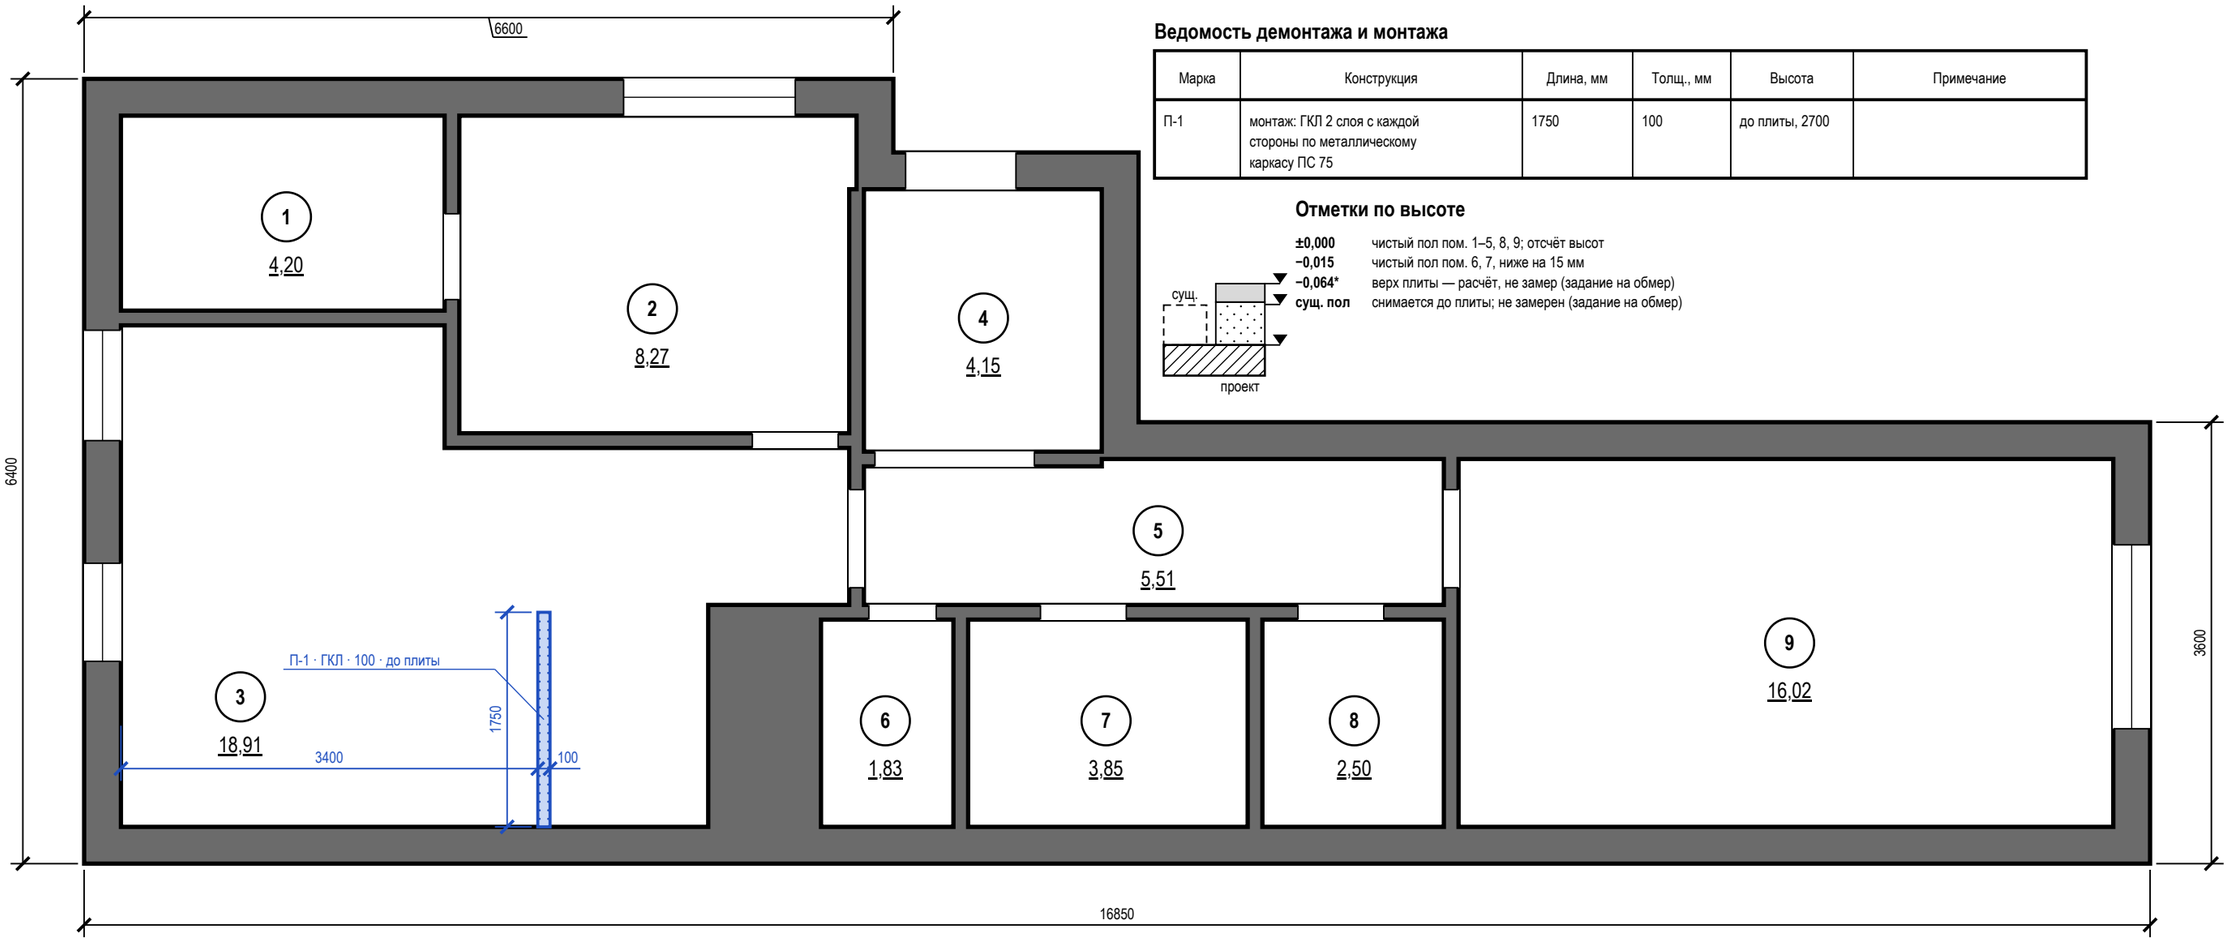

Ведомость демонтажа и монтажа

Марка	Конструкция	Длина, мм	Толщ., мм	Высота	Примечание
П-1	монтаж: ГКЛ 2 слоя с каждой стороны по металлическому каркасу ПС 75	1750	100	до плиты, 2700	

Отметки по высоте

±0,000 чистый пол пом. 1–5, 8, 9; отсчёт высот
−0,015 чистый пол пом. 6, 7, ниже на 15 мм
−0,064* верх плиты — расчёт, не замер (задание на обмер)
сущ. пол снимается до плиты; не замерен (задание на обмер)

Условные обозначения

- существующие стены — сохраняются; несущие не определены — считать несущими
- демонтируемые конструкции — на плане нет
- новое — возводится по проекту (синим)
- проём существующий, без заполнения (откосы)
- (1) номер помещения, площадь м²

Примечания

1. Демонтаж несущих стен и плит перекрытия не производится.
2. Новые перегородки и фальш-стены (синим) привязаны от капитальных стен и наружного контура; высота — по ведомости («до плиты» — до низа плиты перекрытия); проёмы в них усилить стойками каркаса.
3. Перепланировку согласовать до начала работ (ЖК РФ, ст. 26); план не передавать в работу до допуска главного инженера проекта.
4. Дверные блоки — по плану дверей (лист 23); существующие проёмы не расширяются.
5. Демонтаж существующих покрытий пола, стен и потолка, дверных блоков и сантехприборов (если есть) — до основания; объёмы демонтажа — для справки, по факту на объекте.
6. За отметку ±0,000 принят чистый пол, не существующий (блок отметок). Размеры — в мм по чистовой поверхности стен до отделки.
7. Размеры проверить на месте до начала работ: расхождение с обмером — не более 2 % (иначе — к архитектору).
8. Несущие стены не определены: до технического заключения все стены считать несущими — проёмы, ниши и штробы в них не выполнять.

Допущения и предложения на листе

Основа листа: размеры сняты с растрового плана заказчика без размеров: масштаб восстановлен по площадям помещений (≈ 11,8 мм на пиксель), контрольный обмер не выполнен (К-1); высота потолка 2700 мм принята: на плане заказчика её нет (К-2); толщины стен 300 / 120 мм приняты по плану заказчика, не замерены (К-1); разрешённая мощность 15 кВт принята по типовым ТУ для квартиры, ТУ заказчиком не переданы (К-4); подрайон климата не задан — принят не северный (жилые от 2,5 м) (К-9).
Открытые вопросы и конфликты по листу: К-10.
См. лист открытых вопросов (лист 6, записи К-1, К-2, К-4; лист 7, записи К-9, К-10).

1000 мм · печать 1:1

Изм.	Кол.уч	Лист	№ док.	Подп.	Дата
Разраб.		Кырлан А.С.			14.11.26
Пров.					
ГИП					
Н. контр.					
Утв.					

ГД-2026-007-АИ

Квартира 65 м²

Общая площадь 65,24* м² · * размеры со скана, не замерены (реестр — л. 6–8, К-1)

Дизайн-проект интерьера

Стадия	Лист	Листов
РП	22	117

План демонтажа и монтажа перегородок

М 1:50

Кырлан Александр Сергеевич

выпуск 14.11.2026 № 9cc0b98f36 · стр. 23 из 139


План дверей и ведомость заполнения проёмов

Проёмы, марки заполнения, привязки · размеры в мм

ПРЕДВАРИТЕЛЬНО · не для производства работ · открыто пунктов: 14 (реестр — л. 6–8)

Условные обозначения

- стены (подложка обмера)
- новое — возводится по проекту (синим)
- дверь распашная, дуга открывания
- дверь скрытого монтажа
- дверь входная (полотно толще)
- портал (штрих — перемычка)
- оконный блок
- Д — марка типа (Д-N, ПР-N, ОК-N)
- 1 — номер помещения, площадь м²

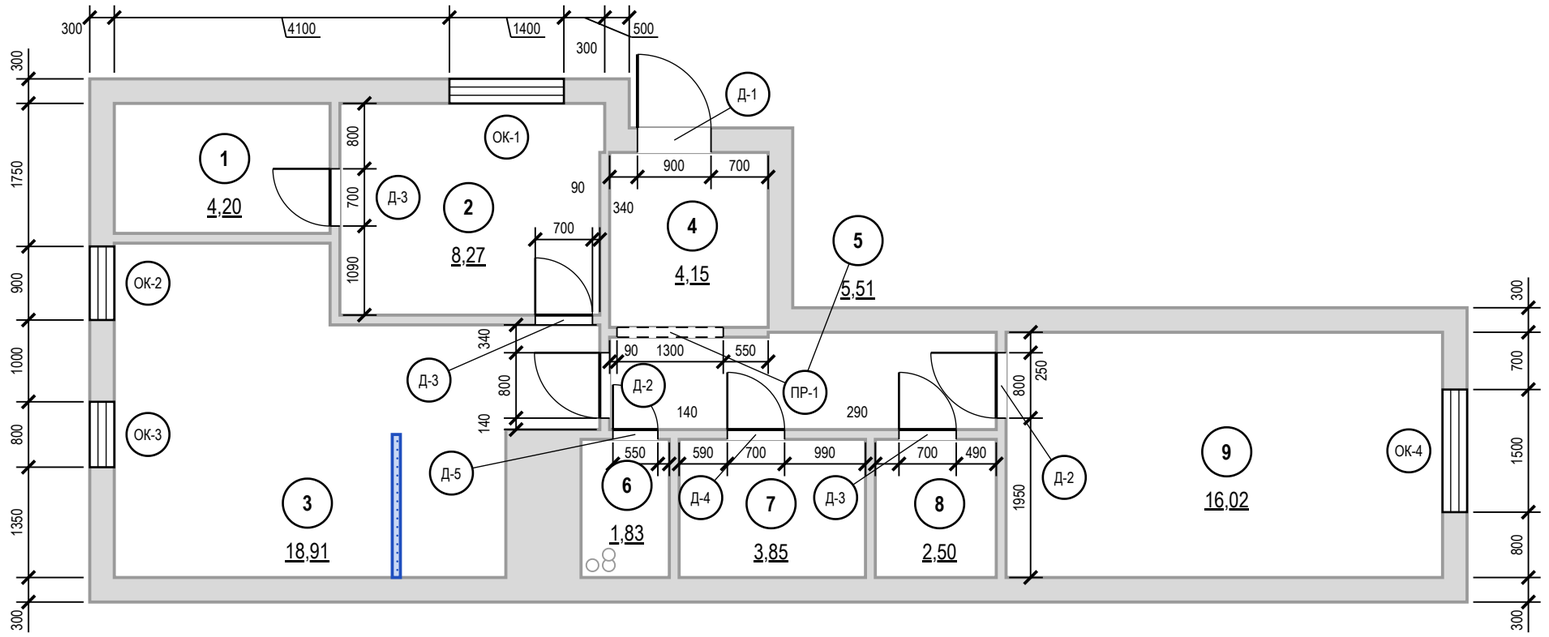

Ведомость заполнения проёмов

Марка	Наименование, обозначение	Проём ш×в, мм	Полотно (расч.)	Кол.	Откр.	Отделка полотна	Фурнитура	Прим.
Д-1	Блок дверной входной, ГОСТ 31173-2016	900×2100	блок задать	1	П	в комплекте блока	в комплекте блока (замки, глазок)	наружу
Д-2	Дверь скрытого монтажа, Profil Doors Invisible	800×2100	700×2050	2	Л, Л	S 1002-Y50R — пом. 3, S 1502-Y50R — пом. 5; S 1502-Y50R — пом. 5, No. 241 — пом. 9	скрытые петли 3D, магнитный замок	
Д-3	Дверь скрытого монтажа, Profil Doors Invisible	700×2100	600×2050	3	Л, П, П	V503 — пом. 1, S 1502-Y50R — пом. 2; S 1502-Y50R — пом. 2, S 1002-Y50R — пом. 3; S 1502-Y50R — пом. 5, S 0502-Y — пом. 8	скрытые петли 3D, магнитный замок	
Д-4	Дверь скрытого монтажа, Profil Doors Invisible	700×2100	600×2050	1	П	S 1502-Y50R — пом. 5, в тон облицовки — пом. 7	скрытые петли 3D, магнитный замок, фиксатор WC	порог 15
Д-5	Дверь скрытого монтажа, Profil Doors Invisible	550×2100	450×2050	1	П	S 1502-Y50R — пом. 5, в тон облицовки — пом. 6	скрытые петли 3D, магнитный замок, фиксатор WC	порог 15
ПР-1	Портал без заполнения	1300×2100		1				б/п
ОК-1	Блок оконный, ГОСТ 23166-2021	1400×1600		1				низ 800
ОК-2	Блок оконный, ГОСТ 23166-2021	900×1600		1				низ 800
ОК-3	Блок оконный, ГОСТ 23166-2021	800×1600		1				низ 800
ОК-4	Блок оконный, ГОСТ 23166-2021	1500×1600		1				низ 800

Примечания

1. Размеры проёмов и привязки — в миллиметрах от чистых граней стен до отделки; привязка — от угла того помещения, со стороны которого стоит размер. Размер проёма — ширина × высота от чистого пола 0,000. Размеры на плане — проёмов, не полотен: полотно — в ведомости, коробка — по системе. Откос от угла помещения до проёма с коробкой — не менее 50 мм.
2. Марки в кружках — типы заполнения проёмов (ГОСТ 21.501-2018, п. 5.3.2); одна марка — один типоразмер; количество сверено с планом.
3. Открывание: Л — петли слева, П — справа, если смотреть со стороны, куда открывается полотно (на себя).
4. Скрытые двери (Д-2…Д-5): проём замерить в чистоте; блок заказать до штукатурки (≈ 30 дн.), короб ставить до штукатурки; полотно навесить после чистовой отделки, красить в цвет стен. Порядок практика монтажа, изготовитель подтверждает.
5. Д-2…Д-5 — существующие проёмы, до техзаключения не расширять (К-8).
6. Полотно «расч.» — по проёму и ряду изделия с запасом по каталогам, заказ — по таблице проёмов модели; Д-1: входной блок по ГОСТ 31173-2016 — задать при выборе блока.
7. Д-1: дуга наружу — по плану заказчика, не проверено; блок оставить или заменить — не решено.
8. Размеры проёмов и привязки сняты со скана плана заказчика и на объекте не замерены (обмерный план — лист 21).
9. Экспликация помещений — лист 21; в марках помещений — номер и площадь, м².

Допущения и предложения на листе

Основа листа: размеры сняты с растрового плана заказчика без размеров: масштаб восстановлен по площадям помещений (≈ 11,8 мм на пиксель), контрольный обмер не выполнен (К-1); высота потолка 2700 мм принята: на плане заказчика её нет (К-2); толщины стен 300 / 120 мм приняты по плану заказчика, не замерены (К-1); разрешённая мощность 15 кВт принята по типовым ТУ для квартиры, ТУ заказчиком не переданы (К-4); подрайон климата не задан — принят не северный (жилые от 2,5 м) (К-9).

Открытые вопросы и конфликты по листу: К-8.

См. лист открытых вопросов (лист 6, записи К-1, К-2, К-4; лист 7, записи К-8, К-9).

1000 мм · печать 1:1

Изм.	Кол.уч	Лист	№ док.	Подп.	Дата
Разраб.		Кырлан А.С.			14.11.26
Пров.					
ГИП					
Н. контр.					
Утв.					

ГД-2026-007-АИ

Квартира 65 м²

Общая площадь 65,24* м² · * размеры со скана, не замерены (реестр — л. 6–8, К-1)

Дизайн-проект интерьера

Стадия	Лист	Листов
РП	23	117

План дверей и ведомость заполнения проёмов

М 1:75

Кырлан Александр Сергеевич

выпуск 14.11.2026 № 9cc0b98f36 · стр. 24 из 139

02

Планировочное решение

выпуск 14.11.2026 № 9cc0b98f36 · стр. 25 из 139


Концепция интерьера

Скандинавский · схема нейтральная · 60/30/10 · материалы, образы и зонирование


Идея

Стиль — скандинавский: светло, спокойно, уютно (hygge), естественно, функционально, в меру (lagom). Палитра выведена из выкрасов (колерная карта): база — тёплые нейтрали NCS S 1502-Y50R / S 1002-Y50R на стенах, NCS S 0300-N на потолках, Tikkurila V503 в гардеробной и детской; второй цвет — Farrow & Ball No. 241 (детская) и NCS S 0502-Y (кладовая); акцент — Farrow & Ball No. 30 Hague Blue (стена и текстиль детской). Цветовая схема нейтральная, пропорция 60/30/10: база на стенах и потолках, вторичный цвет — в текстиле и мягкой мебели, акцент точечно.

Мудборд: материалы и фактуры

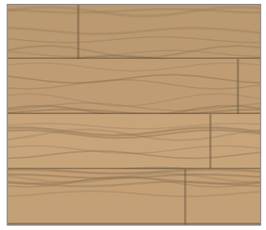

1167-1101
пол

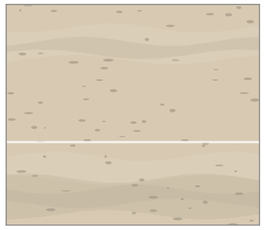

SG501600R
пол



NCS S 0300-N
потолок, плинтус



NCS S 1502-Y50R
стены



Winter · Tikkurila V503
стены, потолок, плинтус



NCS S 1002-Y50R
стены



NCS S 0502-Y
стены



Skimming Stone · Farrow & Ball No. 241
стены, плинтус



Hague Blue · Farrow & Ball No. 30
акцент (стена А)

Палитра 60/30/10

	60 %			30 %		10 %

60 % база — NCS S 1502-Y50R, LRV 72; NCS S 1002-Y50R, LRV 82; NCS S 0300-N, LRV 92; Tikkurila V503 Winter, LRV 86

30 % вторичный — Farrow & Ball No. 241 Skimming Stone, LRV 67; NCS S 0502-Y, LRV 86

10 % акцент — Farrow & Ball No. 30 Hague Blue, LRV 7

Функциональное зонирование (М 1:200)



- дневная зона: гостиная, кухня, столовая
- ночная зона: спальни
- мокрая зона: санузлы
- хранение: гардеробная, кладовая
- вход и коммуникации
- функциональная зона в помещении
- (1) номер помещения (лист 25)

Образы помещений

3. Кухня-гостиная — 18,91 м²

стены NCS S 1002-Y50R
пол — 1167-1101
текстиль: римская штора льняная G503, римская штора льняная G503

2. Спальня — 8,27 м²

стены NCS S 1502-Y50R
пол — 1167-1101
текстиль: римская штора льняная с блэкаут-подкладкой G503, ковёр шерстяной

9. Детская — 16,02 м²

стены Farrow & Ball No. 241; акцент No. 30 на стене А
пол — 1167-1101
текстиль: портьеры H487, тюль V503, ковёр V484

4. Прихожая — 4,15 м²

стены NCS S 1502-Y50R
пол — SG501600R
текстиль: дорожка-коврик хлопковая тканая 800×1400 No. 241

5. Коридор — 5,51 м²

стены NCS S 1502-Y50R
пол — SG501600R
декор: постер в дубовой, постер в дубовой, постер в дубовой

1. Гардеробная — 4,20 м²

стены Tikkurila V503
пол — 1167-1101
свет 3000 K

7. Ванная — 3,85 м²

стены Italon 610010001195
пол — SG501600R
текстиль: полотенца банные махровые No. 299, полотенца для рук вафельные G503, коврик для

6. Санузел — 1,83 м²

стены Italon 610010001195
пол — SG501600R
декор: зеркало над умывальником, постер в тонкой

8. Кладовая — 2,50 м²

стены NCS S 0502-Y
пол — 1167-1101
свет 3000 K

Материалы и отделка

1167-1101
пол — пом. 1, 2, 3, 8, 9

SG501600R
пол — пом. 4, 5, 6, 7

610010001195
стены — пом. 6, 7

Tikkurila V503 Winter, LRV 86
Tikkurila Harmony, матовая
стены, потолок, плинтус — пом. 1, 9

NCS S 1502-Y50R, LRV 72
глубокоматовая
стены — пом. 2, 4, 5

NCS S 0300-N, LRV 92
глубокоматовая
потолок, плинтус — пом. 2, 3, 4, 5, 6, 7, 8

NCS S 1002-Y50R, LRV 82
стены — пом. 3

NCS S 0502-Y, LRV 86
матовая
стены — пом. 8

Farrow & Ball No. 241 Skimming Stone, LRV 67
Farrow & Ball Modern Emulsion, матовая
стены, плинтус — пом. 9

Текстиль и металл

Лён, Tikkurila G503
римская штора льняная с блэкаут-подкладкой, римская штора льняная

Лён, Farrow & Ball No. 231
подушки декоративные на кровать

Шерсть, Farrow & Ball No. 299
плед шерстяной в изножье кровати

Шерсть, NCS S 3020-Y80R
плед шерстяной на диван

Лён, Tikkurila H487
портьеры-волна

Шерсть, NCS S 2002-Y
ковёр шерстяной 2500×1250 под кроватью

Букле, Tikkurila G503
подушка-валик на кровать, подушки на диван

Лён, Farrow & Ball No. 299
подушки на диван, полотенца банные махровые

Шерсть, Farrow & Ball No. 241
дорожка-коврик хлопковая тканая 800×1400, коврик для ванной у бортика ванны

Вуаль, Tikkurila V503
тюль

Чего избегаем

1) Холодный белый + серый ламинат + серый диван без дерева
2) Принты олени/Hygge, надписи, лишние подушки
3) Глянцевый лак на дереве, венге, под орех
4) Одна люстра на комнату, свет 4000–6500 K, споты сеткой
5) Тяжёлые шторы с ламбрекенами, лепнина, многоуровневые потолки
6) Три разных светлых дуба в одном помещении

Допущения и предложения на листе

Основа листа: размеры сняты с растрового плана заказчика без размеров: масштаб восстановлен по площадям помещений (≈ 11,8 мм на пиксель), контрольный обмер не выполнен (К-1); высота потолка 2700 мм принята: на плане заказчика её нет (К-2); толщины стен 300 / 120 мм приняты по плану заказчика, не замерены (К-1); разрешённая мощность 15 кВт принята по типовым ТУ для квартиры, ТУ заказчиком не переданы (К-4); подрайон климата не задан — принят не северный (жилые от 2,5 м) (К-9).
См. лист открытых вопросов (лист 6, записи К-1, К-2, К-4; лист 7, запись К-9).

Примечания

1. Коды цвета — по веерам производителей (колерная карта, лист 58); перед закупкой краски — выкрас на стене объекта под дневным светом и лампами проекта.
2. Материалы — по ведомости отделки (лист 57); мебель, текстиль и декор — по спецификации (лист 26). Образцы доски, керамогранита и тканей утвердить до заказа.
3. Фактуры на листе условные, цвет передан по HEX-значениям производителей: при печати возможны отклонения, решение — только по физическому образцу.

Изм.	Кол.уч	Лист	№ док.	Подп.	Дата
Разраб.		Кырлан А.С.			14.11.26
Пров.					
ГИП					
Н. контр.					
Утв.					

ГД-2026-007-АИ

Квартира 65 м²

Общая площадь 65,24* м² · * размеры со скана, не замерены (реестр — л. 6–8, К-1)

Дизайн-проект интерьера

Стадия	Лист	Листов
РП	24	117

Концепция интерьера
М б/м


Кырлан Александр Сергеевич

выпуск 14.11.2026 № 9cc0b98f36 · стр. 26 из 139

План расстановки мебели

Мебель и оборудование · размеры в мм от чистовых стен · марки — по ведомости

ПРЕДВАРИТЕЛЬНО · не для производства работ · открыто пунктов: 14 (реестр — л. 6–8)

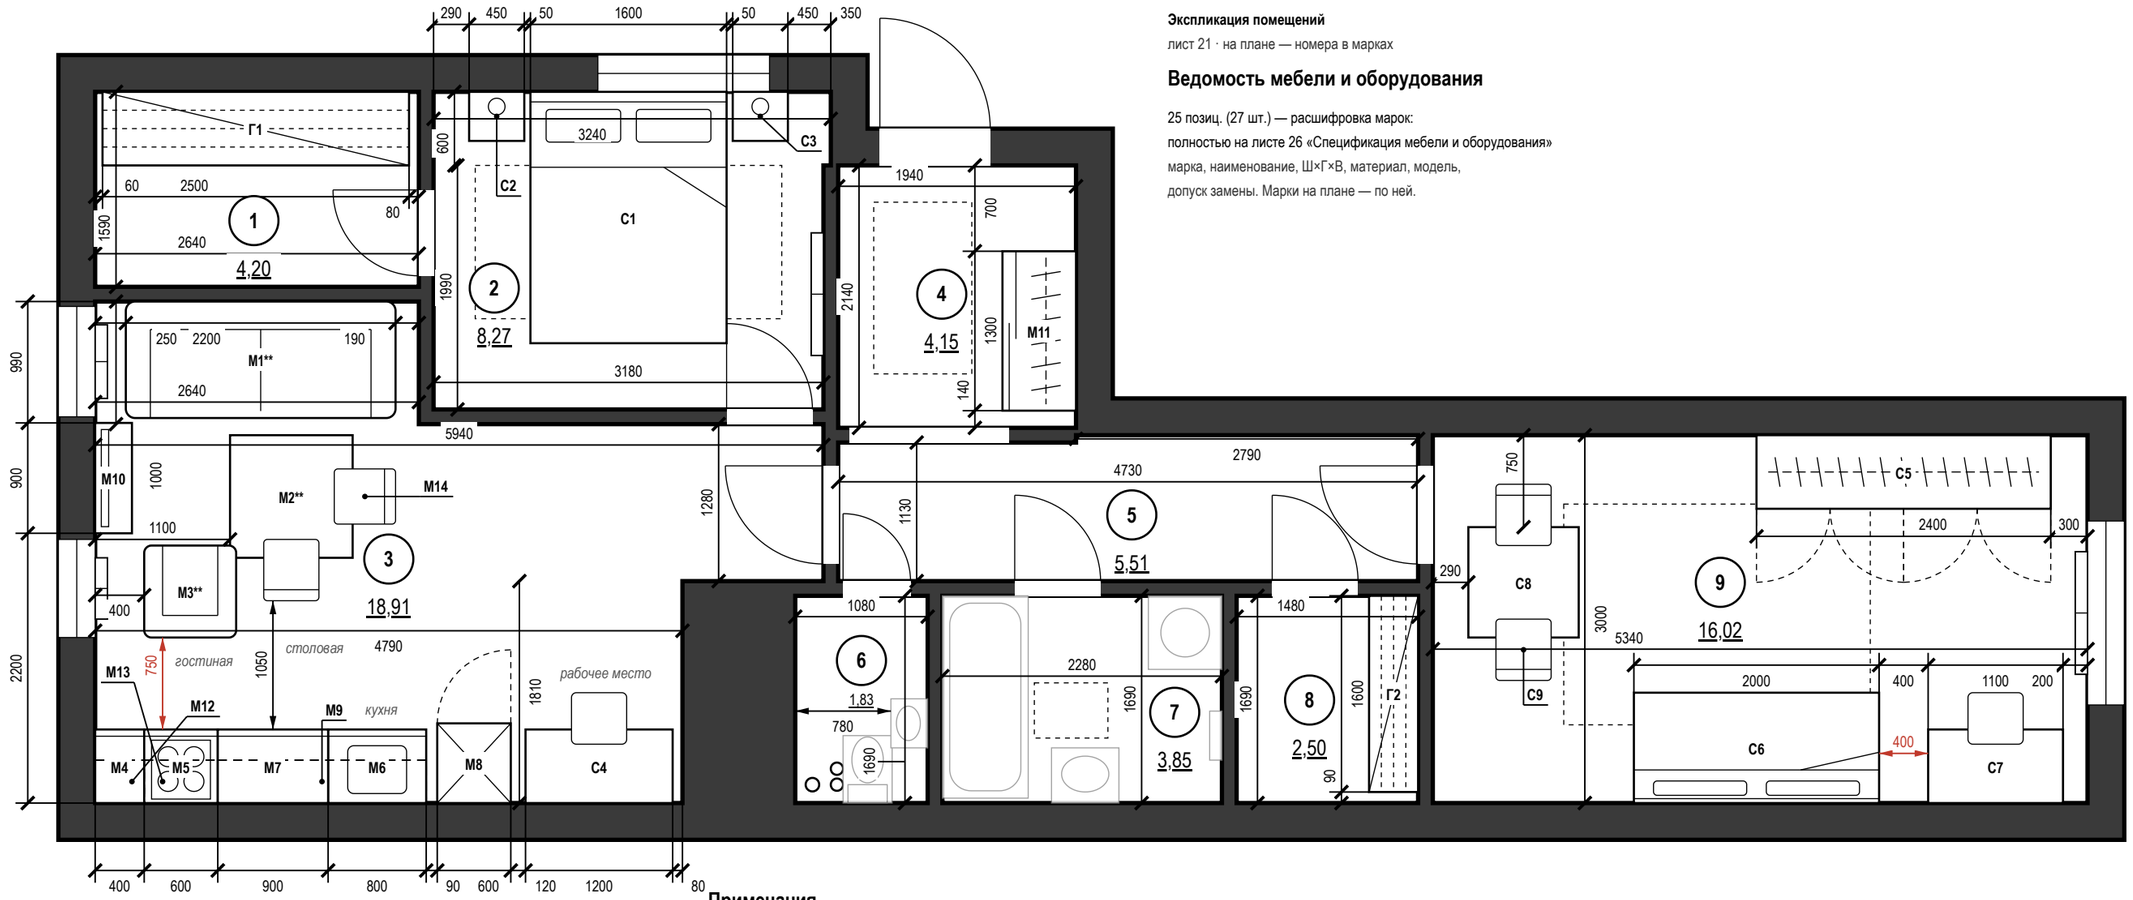

Экспликация помещений

лист 21 · на плане — номера в марках

Ведомость мебели и оборудования

25 позиц. (27 шт.) — расшифровка марок:
полностью на листе 26 «Спецификация мебели и оборудования»
марка, наименование, Ш×Г×В, материал, модель,
допуск замены. Марки на плане — по ней.

Условные обозначения

- мебель и оборудование — габарит в масштабе
- навесные шкафы (низ выше 0,9 м) — невидимый контур
- ковёр
- зона открывания дверец шкафов и техники
- **К1** — марка предмета по ведомости мебели
- привязка от чистовой стены, мм
- ширина прохода, зазор, мм
- проход меньше нормы — расстановку изменить
- сантехприборы — подложка (лист ВК)
- радиатор отопления (лист ОВ)
- существующие стены (сечение)
- стояк: К1 — канализация, В1 — ХВС, Т3 — ГВС
- (1) — номер помещения, площадь м²
- *зона* — функциональная зона помещения

1000 мм · печать 1:1

Допущения и предложения на листе

Основа листа: размеры сняты с растрового плана заказчика без размеров: масштаб восстановлен по площадям помещений (≈ 11,8 мм на пиксель), контрольный обмер не выполнен (К-1); высота потолка 2700 мм принята: на плане заказчика её нет (К-2); толщины стен 300 / 120 мм приняты по плану заказчика, не замерены (К-1); разрешённая мощность 15 кВт принята по типовым ТУ для квартиры, ТУ заказчиком не переданы (К-4); подрайон климата не задан — принят не северный (жилые от 2,5 м) (К-9).
Знак «**» — предложение проектировщика, заказчиком не утверждено (согласовать с заказчиком): К-5: М2 — Было х 1000, у 2700; М3 — Было х 800, у 1750 — место занял диван М1; М1 — Было х 2900, у 3000 — в полосе 1400 мм между спальней и кухней, единственном проходе от двери Д-2: стыки частей 290 / 200 / 0 мм (→).
Открытые вопросы и конфликты по листу: К-1, К-5.
См. лист открытых вопросов (лист 6, записи К-1, К-2, К-4, К-5; лист 7, запись К-9).

Примечания

1. Размеры — в мм от чистовых поверхностей стен, размеры помещений — в свету, привязки — от стен, углов помещения и соседних предметов, проходы и зазоры — стрелками; розетки и выводы под мебель — лист 29, выключатели — лист 31, сантехприборы — лист 39.
2. Общие указания к расстановке (чистовой слой, контрольный обмер, зазоры встроенной мебели, замена покупной) — примечания к спецификации, лист 26.
3. Стулья обеденной группы (М14 — 2 шт., С9 — 2 шт.) показаны в рабочем положении, задвинутыми под столешницу на 150 мм.

Изм.	Кол.уч	Лист	№ док.	Подп.	Дата
Разраб.		Кырлан А.С.			14.11.26
Пров.					
ГИП					
Н. контр.					
Утв.					

ГД-2026-007-АИ

Квартира 65 м²

Общая площадь 65,24* м² · * размеры со скана, не замерены (реестр — л. 6–8, К-1)

Дизайн-проект интерьера

Стадия	Лист	Листов
РП	25	117

План расстановки мебели

М 1:50

Кырлан Александр Сергеевич

выпуск 14.11.2026 № 9cc0b98f36 · стр. 27 из 139

Спецификация мебели и оборудования

ПРЕДВАРИТЕЛЬНО · не для производства работ · открыто пунктов: 14 (реестр — л. 6–8)

Форма 1 ГОСТ 21.110-2013 · позиции мебели — по плану расстановки

Поз.	Наименование и техническая характеристика	Тип, марка, обозначение документа, опросного листа	Код продукции	Поставщик	Ед. измерения	Кол.	Масса 1 ед., кг	Примечание
	Мебель встроенная и корпусная (изготовление по чертежам мебельщика)							
Г1	Система хранения: штанги, полки, ящики; каркас и полки — ЛДСП 16 мм, декор «дуб натуральный»; без фасадов; Ш×Г×В 2500×600×2400 мм	—	—	изготовление на заказ	шт.	1	—	пом. 1; крепление к стене
М4	Модуль нижний; корпус ЛДСП 16 мм; фасады — МДФ эмаль 18 мм; Ш×Г×В 400×600×900 мм	—	—	изготовление на заказ	шт.	1	—	пом. 3
М5	Модуль нижний, варочная; корпус ЛДСП 16 мм; фасады — МДФ эмаль 18 мм; Ш×Г×В 600×600×900 мм	—	—	изготовление на заказ	шт.	1	—	пом. 3
М6	Модуль нижний, мойка; корпус ЛДСП 16 мм; фасады — МДФ эмаль 18 мм; Ш×Г×В 800×600×900 мм	—	—	изготовление на заказ	шт.	1	—	пом. 3
М7	Модуль нижний; корпус ЛДСП 16 мм; фасады — МДФ эмаль 18 мм; Ш×Г×В 900×600×900 мм	—	—	изготовление на заказ	шт.	1	—	пом. 3
М8	Пенал кухонный, холодильник; корпус ЛДСП 16 мм; фасады — без фасада (прибор отдельностоящий); Ш×Г×В 600×650×2100 мм	—	—	изготовление на заказ	шт.	1	—	пом. 3
М9	Модуль навесной; корпус ЛДСП 16 мм; фасады — МДФ эмаль 18 мм; Ш×Г×В 1700×350×720 мм	—	—	изготовление на заказ	шт.	1	—	пом. 3
М12	Навесной модуль; корпус ЛДСП 16 мм; фасады — МДФ эмаль 18 мм; Ш×Г×В 400×350×720 мм	—	—	изготовление на заказ	шт.	1	—	пом. 3
М13	Навесной модуль над варочной, вытяжка встраивается в дно; корпус ЛДСП 16 мм; фасады — МДФ эмаль 18 мм; Ш×Г×В 600×350×620 мм	—	—	изготовление на заказ	шт.	1	—	пом. 3
М11	Шкаф-купе; корпус ЛДСП 16 мм; фасады — ЛДСП 10 мм в алюминиевом профиле; Ш×Г×В 1300×600×2500 мм	—	—	изготовление на заказ	шт.	1	—	пом. 4
Г2	Стеллаж кладовой; каркас и полки — ЛДСП 16 мм, декор «дуб натуральный»; без фасадов; Ш×Г×В 1600×400×2400 мм	—	—	изготовление на заказ	шт.	1	—	пом. 8
С5	Шкаф распашной; корпус ЛДСП 16 мм; фасады — МДФ 18 мм, эмаль матовая; цвет фасадов — в цвет стен (Farrow & Ball No. 241); Ш×Г×В 2400×600×2400 мм	—	—	изготовление на заказ	шт.	1	—	пом. 9
	Мебель покупная							
С1	Кровать двуспальная; мягкое изголовье, обивка — ткань, цвет Farrow & Ball No. 241; Ш×Г×В 1600×2050×450 мм	аналог: Ш×Г×В 1600×2050×450 мм, мягкое изголовье	—	аналог по характеристикам	шт.	1	—	пом. 2; замена ≤ габарита
С2, С3	Тумба прикроватная; шпон, дуб натуральный, матовое масло; Ш×Г×В 450×400×500 мм	аналог: Ш×Г×В 450×400×500 мм, шпон	—	аналог по характеристикам	шт.	2	—	пом. 2; замена ≤ габарита
М1**	Диван; обивка — ткань, цвет Farrow & Ball No. 241; Ш×Г×В 2200×950×850 мм	аналог: Ш×Г×В 2200×950×850 мм, обивка — ткань	—	аналог по характеристикам	шт.	1	—	пом. 3; замена ≤ габарита
М2**	Стол обеденный круглый Ø1000; шпон, дуб натуральный, матовое масло; Ш×Г×В 1000×1000×750 мм	аналог: Ш×Г×В 1000×1000×750 мм, шпон	—	аналог по характеристикам	шт.	1	—	пом. 3; замена ≤ габарита
М3**	Кресло; обивка — ткань, цвет Farrow & Ball No. 241; Ш×Г×В 750×750×800 мм	аналог: Ш×Г×В 750×750×800 мм, обивка — ткань	—	аналог по характеристикам	шт.	1	—	пом. 3; замена ≤ габарита
М10	ТВ на стене, тумба подвесная; шпон, дуб натуральный, матовое масло; Ш×Г×В 900×300×450 мм	аналог: Ш×Г×В 900×300×450 мм, шпон	—	аналог по характеристикам	шт.	1	—	пом. 3; замена ≤ габарита
М14	Стул обеденный к столу М2**; обивка — ткань, цвет Farrow & Ball No. 241; каркас — дуб натуральный; Ш×Г×В 450×500×820 мм	аналог: Ш×Г×В 450×500×820 мм, обивка — ткань	—	аналог по характеристикам	шт.	2	—	пом. 3; замена ≤ габарита
С4	Стол рабочий (кабинет); шпон, дуб натуральный, матовое масло; Ш×Г×В 1200×600×750 мм	аналог: Ш×Г×В 1200×600×750 мм, шпон	—	аналог по характеристикам	шт.	1	—	пом. 3; замена ≤ габарита
С6	Кровать односпальная 900×2000; мягкое изголовье, обивка — ткань, цвет Farrow & Ball No. 241; Ш×Г×В 2000×900×450 мм	аналог: Ш×Г×В 2000×900×450 мм, мягкое изголовье	—	аналог по характеристикам	шт.	1	—	пом. 9; замена ≤ габарита
С7	Стол письменный; шпон, дуб натуральный, матовое масло; Ш×Г×В 1100×600×750 мм	аналог: Ш×Г×В 1100×600×750 мм, шпон	—	аналог по характеристикам	шт.	1	—	пом. 9; замена ≤ габарита
С8	Стол игровой круглый Ø900; шпон, дуб натуральный, матовое масло; Ш×Г×В 900×900×600 мм	аналог: Ш×Г×В 900×900×600 мм, шпон	—	аналог по характеристикам	шт.	1	—	пом. 9; замена ≤ габарита
С9	Стул обеденный к столу С8; обивка — ткань, цвет Farrow & Ball No. 241; каркас — дуб натуральный; Ш×Г×В 450×500×820 мм	аналог: Ш×Г×В 450×500×820 мм, обивка — ткань	—	аналог по характеристикам	шт.	2	—	пом. 9; замена ≤ габарита

Примечания

1. Позиции мебели совпадают с марками на плане расстановки (лист 25); размеры Ш×Г×В — Ш вдоль стены, Г от стены.
2. Размеры и привязки плана расстановки — в мм от чистовых поверхностей стен: слой штукатурки 20 мм по блоку и 5 мм шпаклёвки по ГКЛ учтён; привязки — от стен и углов помещения, а не от другой мебели.
3. План расстановки не является документацией для изготовления мебели. Встроенная и корпусная мебель изготавливается по чертежам мебельщика после контрольного обмера (после штукатурки); «стена в стену» — с зазором 10 мм с каждой стороны или с компенсаторами; графы «Тип, марка» и «Код продукции» для неё не заполняются (ГОСТ 21.110-2013).
4. Покупные изделия — аналог по характеристикам: заменять только на изделия не больше указанного габарита и того же материала и цвета.
5. Материал и цвет, не указанные в данных изделия, приняты по концепции (лист 24): тон дерева — по полу, обивка — по вторичному цвету палитры; образцы согласовать до заказа.
6. Масса 1 ед. для изделий до 25 кг не указывается. Техника — по монтажным схемам изготовителя; выводы — по листам ЭОМ и ВК.

Допущения и предложения на листе

Основа листа: размеры сняты с растрового плана заказчика без размеров: масштаб восстановлен по площадям помещений (≈ 11,8 мм на пиксель), контрольный обмер не выполнен (К-1); высота потолка 2700 мм принята: на плане заказчика её нет (К-2); толщины стен 300 / 120 мм приняты по плану заказчика, не замерены (К-1); разрешённая мощность 15 кВт принята по типовым ТУ для квартиры, ТУ заказчиком не переданы (К-4); подрайон климата не задан — принят не северный (жилые от 2,5 м) (К-9).
Знак «**» — предложение проектировщика, заказчиком не утверждено (согласовать с заказчиком): К-5: М2 — Было х 1000, у 2700; М3 — Было х 800, у 1750 — место занял диван М1; М1 — Было х 2900, у 3000 — в полосе 1400 мм между спальней и кухней, единственном проходе от двери Д-2: стыки частей 290 / 200 / 0 мм (→).
См. лист открытых вопросов (лист 6, записи К-1, К-2, К-4, К-5; лист 7, запись К-9).

Изм.	Кол.уч	Лист	№ док.	Подп.	Дата
Разраб.		Кырлан А.С.			14.11.26
Пров.					
ГИП					
Н. контр.					
Утв.					

ГД-2026-007-АИ

Квартира 65 м²

Общая площадь 65,24* м² · * размеры со скана, не замерены (реестр — л. 6–8, К-1)

Дизайн-проект интерьера

Стадия	Лист	Листов
РП	26	117

Спецификация мебели и оборудования

М б/м

Кырлан Александр Сергеевич

выпуск 14.11.2026 № 9cc0b98f36 · стр. 28 из 139

Спецификация мебели и оборудования (продолжение)

ПРЕДВАРИТЕЛЬНО · не для производства работ · открыто пунктов: 14 (реестр — л. 6–8)

Форма 1 ГОСТ 21.110-2013 · позиции мебели — по плану расстановки

Поз.	Наименование и техническая характеристика	Тип, марка, обозначение документа, опросного листа	Код продукции	Поставщик	Ед. измерения	Кол.	Масса 1 ед., кг	Примечание
	Техника встраиваемая и бытовая (покупные изделия), светильники под розетки							
	Холодильник, в модуле М8	аналог по характеристикам: отдельностоящий, габарит — по проёму	—	по выбору заказчика до изготовления мебели	шт.	1	—	пом. 3; по схеме изготовителя
	Варочная панель встраиваемая, индукционная, в модуле М5	аналог по характеристикам: индукционная 60 см, вырез 560 × 490 мм по шаблону модели	—	по выбору заказчика до изготовления мебели	шт.	1	—	пом. 3; по схеме изготовителя
	Вытяжка встраиваемая, в модуле М13	аналог по характеристикам: производительность — по расчёту ОВ, шум ≤ 55 дБ(А)	—	по выбору заказчика до изготовления мебели	шт.	1	—	пом. 3; по схеме изготовителя
	Стиральная машина, место по листу ВК (П22); Ш×Г 600×600 мм	аналог по характеристикам: тип загрузки — по листу ВК, в плане 600 × 600 мм (ширина × глубина), по листу ВК	—	по выбору заказчика до изготовления мебели	шт.	1	—	пом. 7; по схеме изготовителя
	Торшер, у поз. М3**; абажур — ткань или опаловое стекло; лампа 3000 К	—	—	аналог по характеристикам	шт.	1	—	пом. 3; розетка — по плану розеток (ЭОМ)
	Торшер, у поз. С6; абажур — ткань или опаловое стекло; лампа 2700 К	—	—	аналог по характеристикам	шт.	1	—	пом. 9; розетка Р11 (ЭОМ)
	Текстиль							
Т6**	Римская штора льняная с блэкаут-подкладкой, молочная; лён 100 %; цвет Tikkurila G503; карниз 1500 мм, высота 1750 мм	—	—	аналог по характеристикам	шт.	1	—	пом. 2
Т13**	Ковёр шерстяной 2500×1250 под кроватью, выходит по бокам на 450 мм, овсяный; шерсть 100 %; цвет NCS S 2002-Y; 2500×1250 мм	—	—	аналог по характеристикам	шт.	1	—	пом. 2; с подложкой
Т14**	Подушки декоративные на кровать, лён, пыльно-розовый; лён 100 %; цвет Farrow & Ball No. 231	—	—	аналог по характеристикам	шт.	2	—	пом. 2
Т15**	Подушка-валик на кровать, букле молочное; букле (шерсть 60 %, полиэстер 40 %); цвет Tikkurila G503	—	—	аналог по характеристикам	шт.	1	—	пом. 2
Т16**	Плед шерстяной в изножье кровати, приглушённый синий; шерсть мериноса 100 %; цвет Farrow & Ball No. 299	—	—	аналог по характеристикам	шт.	1	—	пом. 2
Т1**	Римская штора льняная, молочная (окно 1); лён 100 %; цвет Tikkurila G503; карниз 1000 мм, высота 1750 мм	—	—	аналог по характеристикам	шт.	1	—	пом. 3
Т2**	Римская штора льняная, молочная (окно 2); лён 100 %; цвет Tikkurila G503; карниз 900 мм, высота 1750 мм	—	—	аналог по характеристикам	шт.	1	—	пом. 3
Т3**	Подушки на диван, букле молочное; букле (шерсть 60 %, полиэстер 40 %); цвет Tikkurila G503	—	—	аналог по характеристикам	шт.	3	—	пом. 3
Т4**	Подушки на диван, лён, приглушённый синий; лён 100 %; цвет Farrow & Ball No. 299	—	—	аналог по характеристикам	шт.	2	—	пом. 3
Т5**	Плед шерстяной на диван, терракота; шерсть мериноса 100 %; цвет NCS S 3020-Y80R	—	—	аналог по характеристикам	шт.	1	—	пом. 3
Т17**	Ковёр — дорожка-коврик хлопковая тканая 800×1400, светлая; хлопок 100 %; цвет Farrow & Ball No. 241; 800×1400 мм	—	—	аналог по характеристикам	шт.	1	—	пом. 4; с подложкой
Т18**	Полотенца банные махровые, приглушённый синий, сложены на полотенцесушителе; хлопок 100 %; цвет Farrow & Ball No. 299	—	—	аналог по характеристикам	шт.	2	—	пом. 7
Т19**	Полотенца для рук вафельные, молочные, на нижних перекладинах сушителя; хлопок 100 %; цвет Tikkurila G503	—	—	аналог по характеристикам	шт.	2	—	пом. 7
Т20**	Ковёр — коврик для ванной у бортика ванны, хлопок тафтинг, светлый каменный; хлопок 100 %, латексная противоскользящая основа; цвет Farrow & Ball No. 241; 600×450 мм	—	—	аналог по характеристикам	шт.	1	—	пом. 7; с подложкой
Т7	Портьеры-волна; лён 100 %; цвет Tikkurila H487; карниз 1820 мм, высота 2590 мм, сборка 2	—	—	аналог по характеристикам	шт.	2	—	пом. 9
Т8	Тюль; полиэстер 100 %; цвет Tikkurila V503; карниз 1820 мм, высота 2590 мм, сборка 2,5	—	—	аналог по характеристикам	шт.	1	—	пом. 9

Допущения и предложения на листе

Основа листа: размеры сняты с растрового плана заказчика без размеров: масштаб восстановлен по площадям помещений (≈ 11,8 мм на пиксель), контрольный обмер не выполнен (К-1); высота потолка 2700 мм принята: на плане заказчика её нет (К-2); толщины стен 300 / 120 мм приняты по плану заказчика, не замерены (К-1); разрешённая мощность 15 кВт принята по типовым ТУ для квартиры, ТУ заказчиком не переданы (К-4); подрайон климата не задан — принят не северный (жилые от 2,5 м) (К-9).

Знак «**» — предложение проектировщика, заказчиком не утверждено (согласовать с заказчиком): ИЗ-4: Т6, Т13, Т14, Т15, Т16, Т1, Т2, Т3, Т4, Т5, Т17; ИЗ-5: Т18, Т19, Т20; К-5: М3 — Было х 800, у 1750 — место занял диван М1.

См. лист открытых вопросов (лист 6, записи К-1, К-2, К-4, К-5; лист 7, запись К-9; лист 8, записи ИЗ-4, ИЗ-5).

Изм.	Кол.уч	Лист	№ док.	Подп.	Дата
Разраб.		Кырлан А.С.			14.11.26
Пров.					
ГИП					
Н. контр.					
Утв.					

ГД-2026-007-АИ

Квартира 65 м²

Общая площадь 65,24* м² · * размеры со скана, не замерены (реестр — л. 6–8, К-1)

Дизайн-проект интерьера	Стадия	Лист	Листов
	РП	27	117
Спецификация мебели и оборудования (продолжение) М б/м	**Кырлан Александр Сергеевич**		

Спецификация мебели и оборудования (продолжение)

Форма 1 ГОСТ 21.110-2013 · позиции мебели — по плану расстановки

Поз.	Наименование и техническая характеристика	Тип, марка, обозначение документа, опросного листа	Код продукции	Поставщик	Ед. измерения	Кол.	Масса 1 ед., кг	Примечание
Т9	Ковёр под кроватью; шерсть 100 %; цвет Tikkurila V484; 2500×1800 мм	—	—	аналог по характеристикам	шт.	1	—	пом. 9; с подложкой
Т10	Подушки декоративные на кровать; букле (шерсть 60 %, полиэстер 40 %); цвет Farrow & Ball No. 229	—	—	аналог по характеристикам	шт.	3	—	пом. 9
Т11	Подушки на кровать, акцент; хлопковый бархат 100 %; цвет Farrow & Ball No. 47	—	—	аналог по характеристикам	шт.	2	—	пом. 9
Т12	Плед на кровать; шерсть мериноса 100 %; цвет Farrow & Ball No. 30	—	—	аналог по характеристикам	шт.	1	—	пом. 9
	Декор							
ДК6**	Картина напротив кровати: акварель в паспарту, дубовая рама 1000×700; 1000×700 мм; центр на 1500 мм от пола	—	—	аналог по характеристикам	шт.	1	4	пом. 2; крепление: дюбель с крюком, 2 точки
ДК7**	Зеркало в рост в тонкой дубовой раме 500×1600; 500×1600 мм; низ на 300 мм от пола	—	—	аналог по характеристикам	шт.	1	12	пом. 2; крепление: анкер для пустотелых оснований, 4 шт.
ДК1**	Картина над диваном: абстракция, холст в тонкой дубовой раме 1400×900; 1400×900 мм; низ на 1050 мм от пола	—	—	аналог по характеристикам	шт.	1	6	пом. 3; крепление: анкер, 2 шт.
ДК2**	Сансевиерия в напольном керамическом кашпо Ø300, матовый белый; 350×350 мм	—	—	аналог по характеристикам	шт.	1	—	пом. 3
ДК5**	Ваза керамическая матовая с сухой веткой на обеденном столе, молочная; 200×300 мм; на М2**	—	—	аналог по характеристикам	шт.	1	—	пом. 3
ДК8**	Зеркало в рост в дубовой раме 500×1600; 500×1600 мм; низ на 300 мм от пола	—	—	аналог по характеристикам	шт.	1	12	пом. 4; крепление: анкер для пустотелых оснований, 4 шт.
ДК9**	Постер в дубовой раме 400×560, левый (группа «триптих»): графика тушью; 400×560 мм; центр на 1500 мм от пола	—	—	аналог по характеристикам	шт.	1	2	пом. 5; крепление: дюбель с крюком, 2 точки
ДК10**	Постер в дубовой раме 400×560, средний (группа «триптих»): графика тушью; 400×560 мм; центр на 1500 мм от пола	—	—	аналог по характеристикам	шт.	1	2	пом. 5; крепление: дюбель с крюком, 2 точки
ДК11**	Постер в дубовой раме 400×560, правый (группа «триптих»): графика тушью; 400×560 мм; центр на 1500 мм от пола	—	—	аналог по характеристикам	шт.	1	2	пом. 5; крепление: дюбель с крюком, 2 точки
ДК12**	Зеркало над умывальником, влагостойкое, в тонкой дубовой раме 400×600; 400×600 мм; низ на 1150 мм от пола	—	—	аналог по характеристикам	шт.	1	5	пом. 6; крепление: клей для зеркал + 2 опорных уголка снизу
ДК14**	Постер в тонкой дубовой раме 300×400: чайка над водой, линейный рисунок; 300×400 мм; низ на 1300 мм от пола	—	—	аналог по характеристикам	шт.	1	1	пом. 6; крепление: дюбель с крюком, 1 точка
ДК13**	Зеркало над умывальником, влагостойкое, в тонкой дубовой раме 550×650; 550×650 мм; низ на 1150 мм от пола	—	—	аналог по характеристикам	шт.	1	5	пом. 7; крепление: клей для зеркал + 2 опорных уголка снизу
ДК3	Картина над кроватью: графика в паспарту, рама — дуб; 1000×700 мм; низ на 1300 мм от пола	—	—	аналог по характеристикам	шт.	1	4	пом. 9; крепление к стене
ДК4	Зеркало в рост в тонкой чёрной раме; рама — чёрный матовый; 600×1600 мм; низ на 300 мм от пола	—	—	аналог по характеристикам	шт.	1	12	пом. 9; крепление: анкер для пустотелых оснований, 4 шт.

Допущения и предложения на листе

Основа листа: размеры сняты с растрового плана заказчика без размеров: масштаб восстановлен по площадям помещений (≈ 11,8 мм на пиксель), контрольный обмер не выполнен (К-1); высота потолка 2700 мм принята: на плане заказчика её нет (К-2); толщины стен 300 / 120 мм приняты по плану заказчика, не замерены (К-1); разрешённая мощность 15 кВт принята по типовым ТУ для квартиры, ТУ заказчиком не переданы (К-4); подрайон климата не задан — принят не северный (жилые от 2,5 м) (К-9).

Знак «**» — предложение проектировщика, заказчиком не утверждено (согласовать с заказчиком): ИЗ-4: ДК6, ДК7, ДК1, ДК2, ДК5, ДК8, ДК9, ДК10, ДК11, ДК12, ДК13; ИЗ-5: ДК14; К-5: М2 — Было х 1000, у 2700.

См. лист открытых вопросов (лист 6, записи К-1, К-2, К-4, К-5; лист 7, запись К-9; лист 8, записи ИЗ-4, ИЗ-5).

Изм.	Кол.уч	Лист	№ док.	Подп.	Дата
Разраб.		Кырлан А.С.			14.11.26
Пров.					
ГИП					
Н. контр.					
Утв.					

ГД-2026-007-АИ

Квартира 65 м²

Общая площадь 65,24* м² · * размеры со скана, не замерены (реестр — л. 6–8, К-1)

	Стадия	Лист	Листов
Дизайн-проект интерьера	РП	28	117
Спецификация мебели и оборудования (продолжение) М б/м	**Кырлан Александр Сергеевич**		

03

Электрооборудование


Кырлан Александр Сергеевич

выпуск 14.11.2026 · 9cc0b98f36 · стр. 31 из 139

План розеток и электровыводов

Розетки, выводы кабеля, щит · размеры в мм · высоты от чистого пола

План розеток (М 1:50)

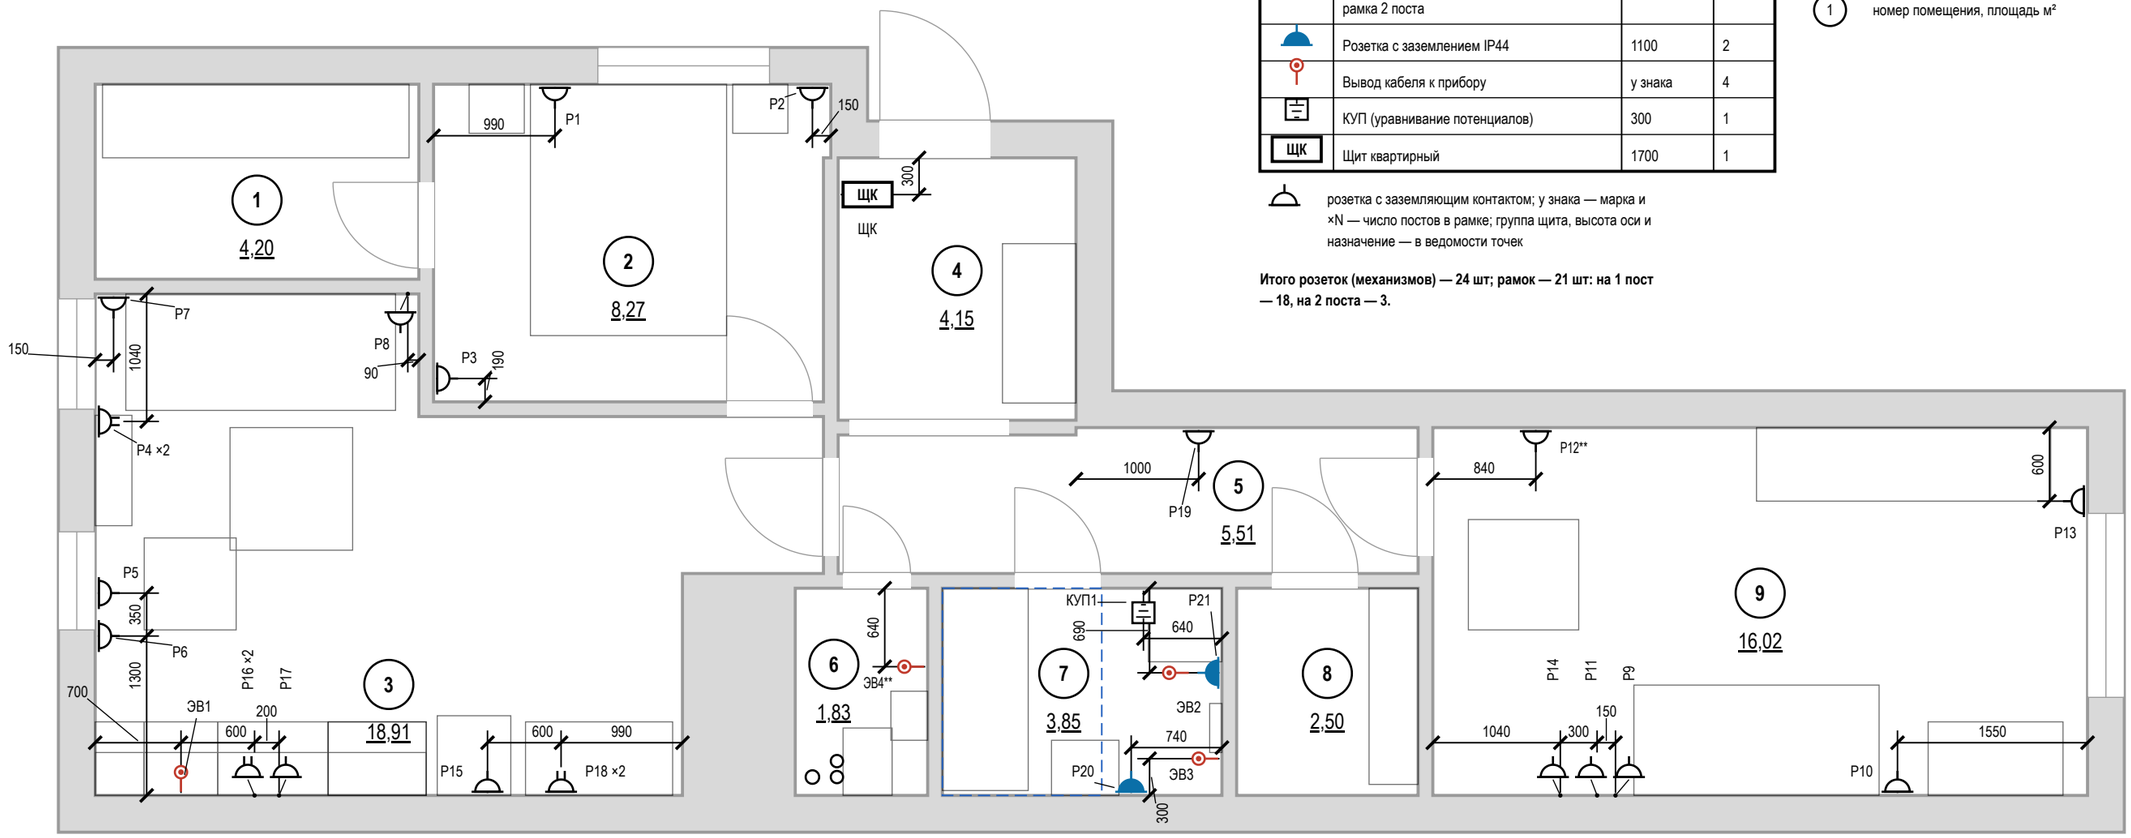

Условные обозначения

Знак	Тип изделия	H, мм	Кол., шт
	Розетка с заземлением	300	10
	То же	у знака	6
	Блок розеток с заземлением, рамка 2 поста	у знака	3
	Розетка с заземлением IP44	1100	2
	Вывод кабеля к прибору	у знака	4
	КУП (уравнивание потенциалов)	300	1
ЩК	Щит квартирный	1700	1

розетка с заземляющим контактом; у знака — марка и ×N — число постов в рамке; группа щита, высота оси и назначение — в ведомости точек

Итого розеток (механизмов) — 24 шт; рамок — 21 шт: на 1 пост — 18, на 2 поста — 3.

Условные обозначения (окончание)

- знак разведён для читаемости: точка на стене — у выноски, привязка — до неё
- граница зоны 2 ванной (600 мм от ванны/поддона)
- мебель и сантехприборы — подложка
- стояк: К1 — канализация, В1 — ХВС, Т3 — ГВС
- 1 — номер помещения, площадь м²

Допущения и предложения на листе

Основа листа: размеры сняты с растрового плана заказчика без размеров: масштаб восстановлен по площадям помещений (≈ 11,8 мм на пиксель), контрольный обмер не выполнен (К-1); высота потолка 2700 мм принята: на плане заказчика её нет (К-2); толщины стен 300 / 120 мм приняты по плану заказчика, не замерены (К-1); разрешённая мощность 15 кВт принята по типовым ТУ для квартиры, ТУ заказчиком не переданы (К-4); подрайон климата не задан — принят не северный (жилые от 2,5 м) (К-9).

Знак «**» — предложение проектировщика, заказчиком не утверждено (согласовать с заказчиком): P12 — Было: стена В смещение 1985, назначение «ТВ над комодом» — над кроватью С6, ТВ2 и LAN4 при этом на стене А, комода в помещении нет (назначение по шаблону); ЭВ4 — вывод к бытовому вентилятору, таймер выбега.

Открытые вопросы и конфликты по листу: К-4.

См. лист открытых вопросов (лист 6, записи К-1, К-2, К-4; лист 7, запись К-9).

Примечания

1. За отметку 0,000 принят уровень чистого пола. Высоты H — от чистого пола до оси изделия; привязки — от чистовой грани стены до оси механизма (у рамки на несколько постов — до оси рамки).
2. Высоты H и группы щита — в ведомости электроточек: розетки — 300 мм от чистого пола до оси механизма, если в ведомости не указано иное; выводы кабеля — по паспорту прибора.
3. Розетки в санузле — только вне зон 0–2 (ПУЭ 7.1.48, ГОСТ Р 50571.7.701-2024), IP44, через УЗО 30 мА.
4. Розеточные и мокрые линии — через УЗО или дифавтомат с током утечки не более 30 мА (ПУЭ 7.1.79); в санузле выполнить ДСУП (ПУЭ 7.1.87–7.1.88).
5. Кабель — медный, исполнение нг(А)-LS (ГОСТ 31565-2012); скрытая прокладка только горизонтально и вертикально, фактические трассы зафиксировать исполнительной схемой до закрытия отделкой.
6. Расчёт нагрузок, токов КЗ, селективности и сечений — по проекту ЭОМ организации с допуском СРО; лист задаёт состав, расположение и группы.
7. Выводы кухонной техники — после утверждения проекта кухни (ориентировочно); привязки выводов даны от осей модулей гарнитура и пересматриваются вместе с проектом кухни.
8. Ведомости электроточек, изделий, светильников и расшифровка клавиш — лист 32.

1000 мм · печать 1:1

Изм.	Кол.уч	Лист	№ док.	Подп.	Дата
Разраб.		Кырлан А.С.			14.11.26
Пров.					
ГИП					
Н. контр.					
Утв.					

ГД-2026-007-АИ

Квартира 65 м²

Общая площадь 65,24* м² · * размеры со скана, не замерены (реестр — л. 6–8, К-1)

Дизайн-проект интерьера

Стадия	Лист	Листов
РП	29	117

План розеток и электровыводов

М 1:50

Кырлан Александр Сергеевич


выпуск 14.11.2026 № 9cc0b98f36 · стр. 32 из 139

План освещения

Светильники, группы включения, извещатели · размеры в мм

План освещения (М 1:50)

ПРЕДВАРИТЕЛЬНО · не для производства работ · открыто пунктов: 14 (реестр — л. 6–8)

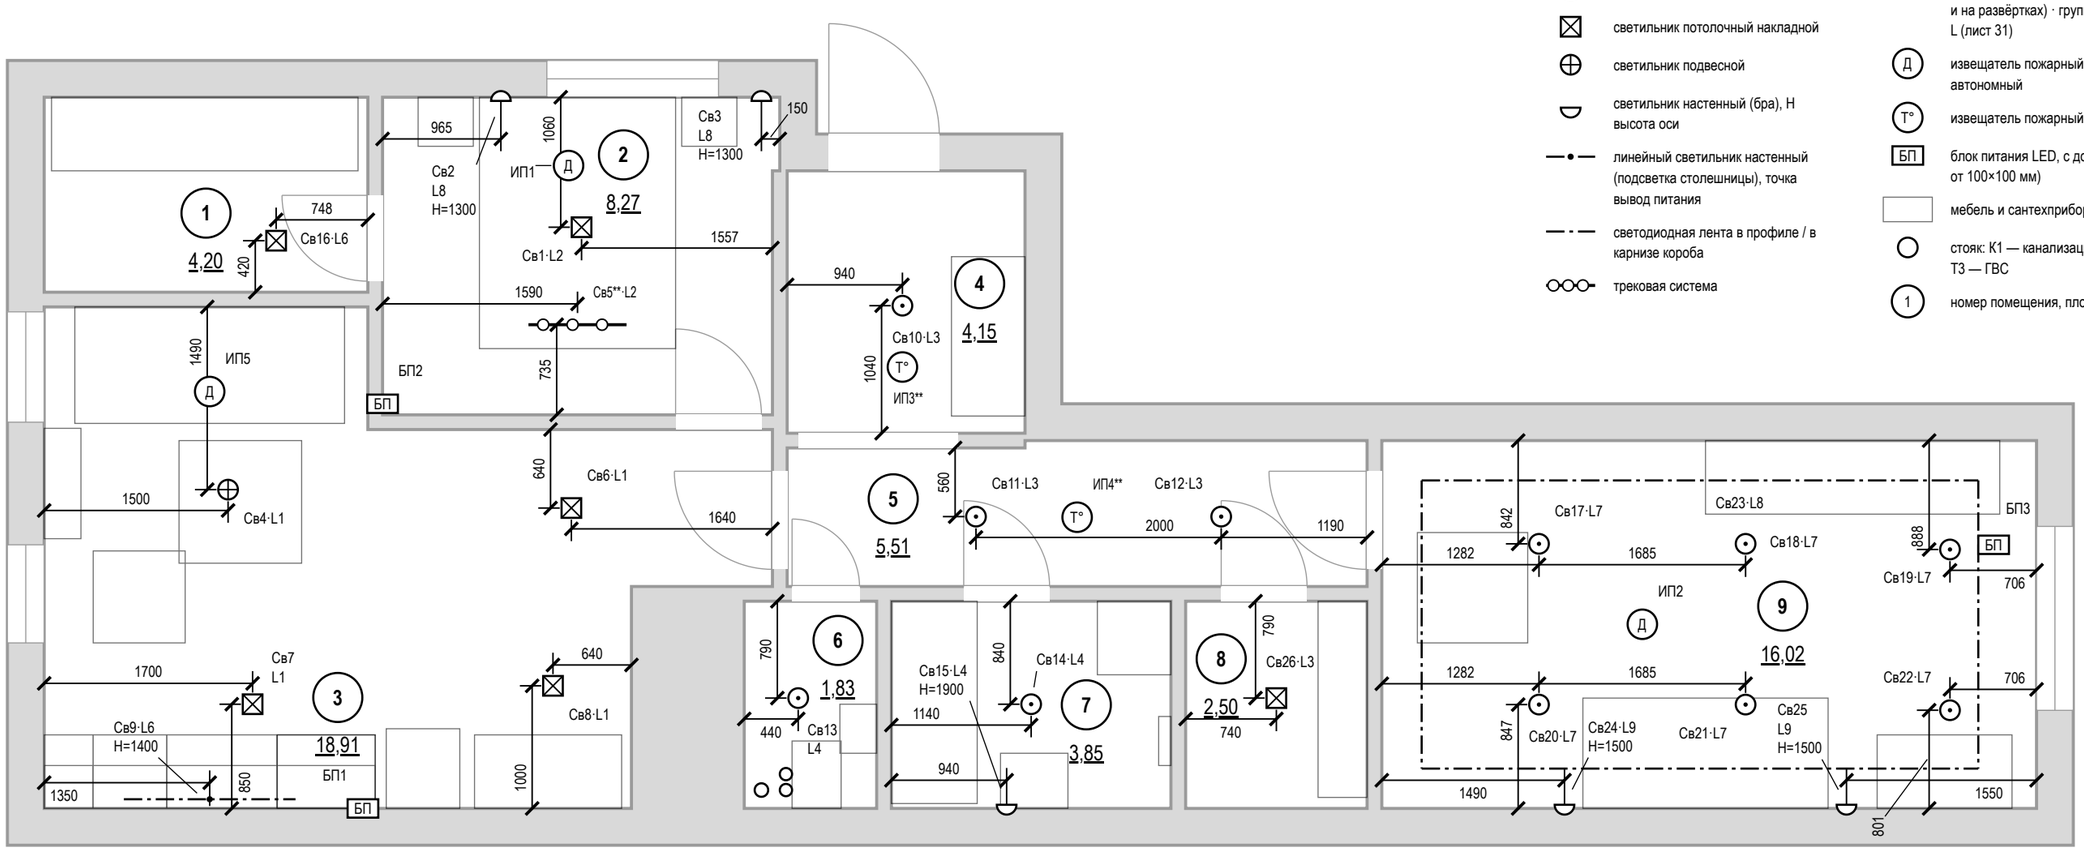

Условные обозначения

- светильник встраиваемый точечный
- светильник потолочный накладной
- светильник подвесной
- светильник настенный (бра), H высота оси
- линейный светильник настенный (подсветка столешницы), точка вывод питания
- светодиодная лента в профиле / в карнизе короба
- трековая система
- Св1·L1 — марка светильника (как в ведомости и на развёртках) · группа включения L (лист 31)
- Д — извещатель пожарный дымовой автономный
- Т° — извещатель пожарный тепловой
- БП — блок питания LED, с доступом (люк от 100×100 мм)
- мебель и сантехприборы — подложка
- стояк: К1 — канализация, В1 — ХВС, Т3 — ГВС
- 1 — номер помещения, площадь м²

Допущения и предложения на листе

Основа листа: размеры сняты с растрового плана заказчика без размеров: масштаб восстановлен по площадям помещений (≈ 11,8 мм на пиксель), контрольный обмер не выполнен (К-1); высота потолка 2700 мм принята: на плане заказчика её нет (К-2); толщины стен 300 / 120 мм приняты по плану заказчика, не замерены (К-1); разрешённая мощность 15 кВт принята по типовым ТУ для квартиры, ТУ заказчиком не переданы (К-4); подрайон климата не задан — принят не северный (жилые от 2,5 м) (К-9).

Знак «**» — предложение проектировщика, заказчиком не утверждено (согласовать с заказчиком): Св5 — трековая система 2 × 900 лм: светильник добавлен проектировщиком, поток принят до нормы освещённости, модель и паспорт не выбраны; ИП3, ИП4 — прихожая / кухня квартиры — тепловой (СП 484, прил. Б, Б.4); место — центр помещения, не ближе 500 мм к светильнику.

См. лист открытых вопросов (лист 6, записи К-1, К-2, К-4; лист 7, запись К-9).

Примечания

1. За отметку 0,000 принят уровень чистого пола. Высоты H — от чистого пола до оси изделия; привязки — от чистовой грани стены до оси механизма (у рамки на несколько постов — до оси рамки).
2. Высота установки, не указанная на плане: светильники — на потолке; настенные — по отметке H у знака. Привязки — до оси светильника от чистовой грани стены, по рядам.
3. Во влажных помещениях — светильники не ниже IP44; в зонах 0–2 ванной — по ГОСТ Р 50571.7.701-2024 (зона 1 — IPX5).
4. LED-лента в карнизе подсветки короба — по линии карниза с плана потолков; блок питания — в люке короба (БП на плане), питание ленты длиннее 5 м — с двух концов.
5. Розеточные и мокрые линии — через УЗО или дифавтомат с током утечки не более 30 мА (ПУЭ 7.1.79); в санузле выполнить ДСУП (ПУЭ 7.1.87–7.1.88).
6. Кабель — медный, исполнение нг(A)-LS (ГОСТ 31565-2012); скрытая прокладка только горизонтально и вертикально, фактические трассы зафиксировать исполнительной схемой до закрытия отделкой.
7. Расчёт нагрузок, токов КЗ, селективности и сечений — по проекту ЭОМ организации с допуском СРО; лист задаёт состав, расположение и группы.
8. Ведомость светильников (тип, количество, мощность, поток, Tц, Ra) — лист 48.
9. Оценка освещённости (по норме СанПиН 1.2.3685-21, табл. 5.52, на полу; не светотехнический расчёт, декоративная подсветка в оценку не входит) — лист 32.

1000 мм · печать 1:1

Изм.	Кол.уч	Лист	№ док.	Подп.	Дата
Разраб.		Кырлан А.С.			14.11.26
Пров.					
ГИП					
Н. контр.					
Утв.					

ГД-2026-007-АИ

Квартира 65 м²

Общая площадь 65,24* м² · * размеры со скана, не замерены (реестр — л. 6–8, К-1)

Дизайн-проект интерьера

Стадия	Лист	Листов
РП	30	117

План освещения

М 1:50

Кырлан Александр Сергеевич


выпуск 14.11.2026 № 9cc0b98f36 · стр. 33 из 139

План выключателей и схема включения

ПРЕДВАРИТЕЛЬНО · не для производства работ · открыто пунктов: 14 (реестр — л. 6–8)

Выключатели S, группы включения L, линии связи · размеры в мм

План выключателей (М 1:50)

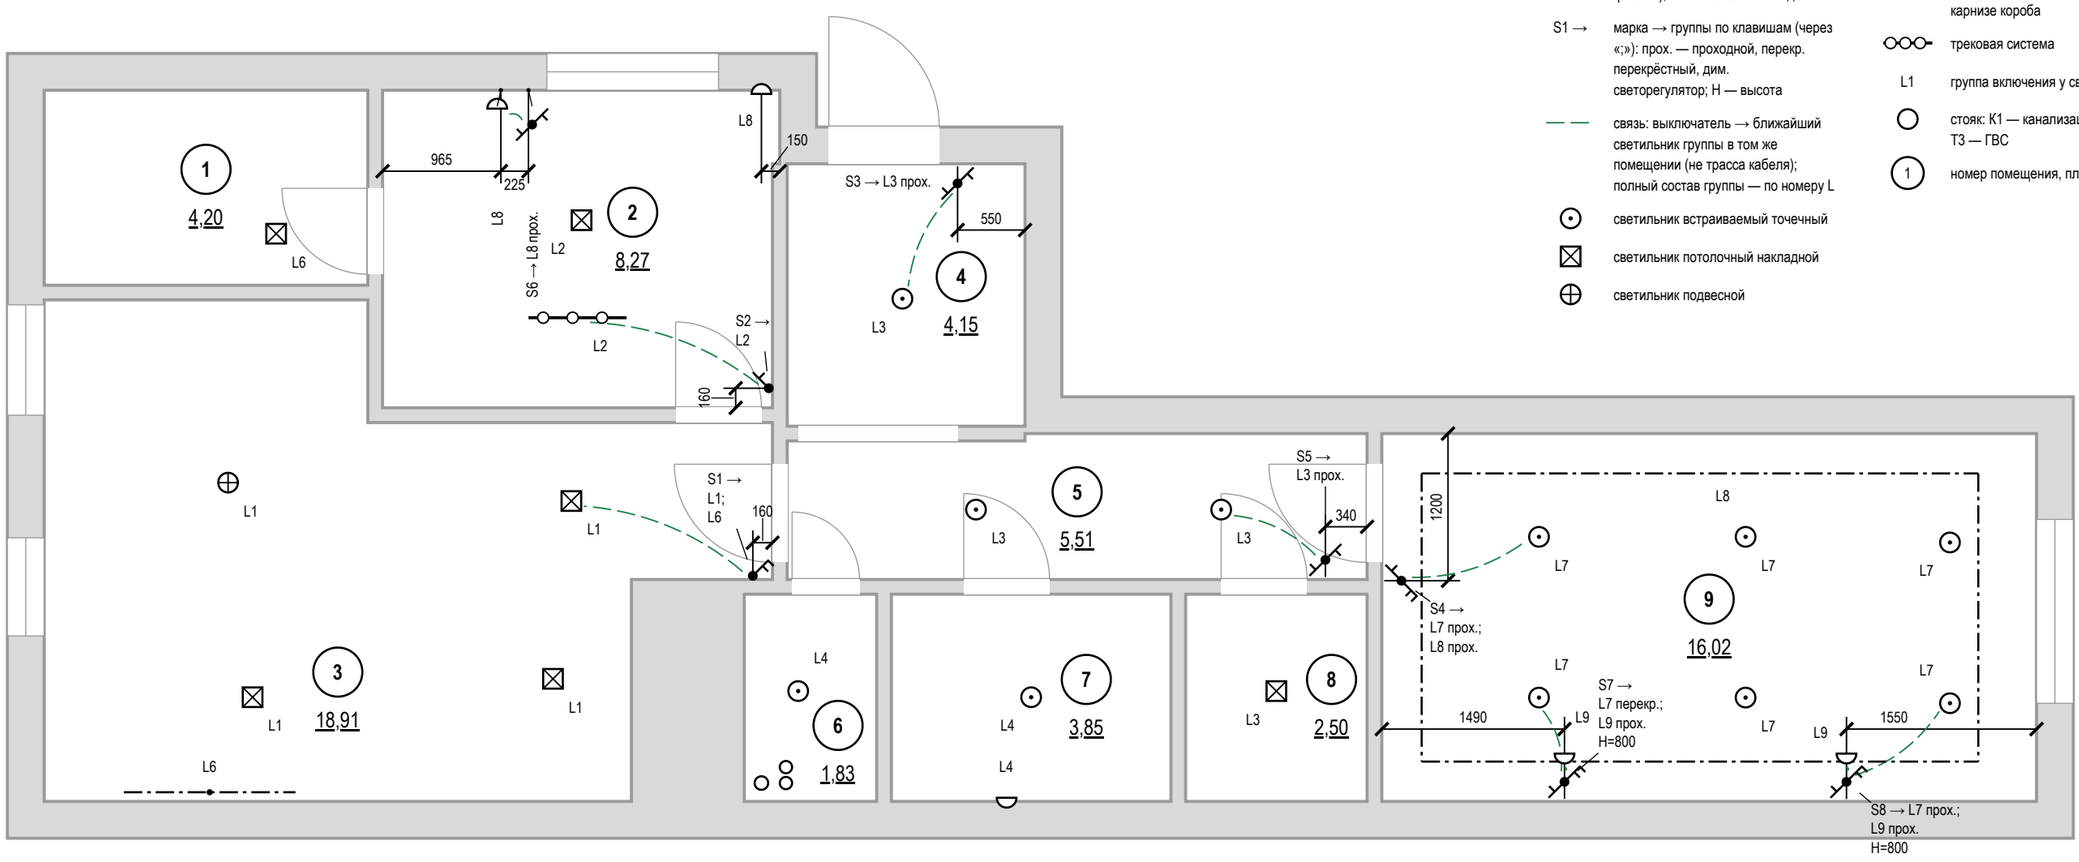

Условные обозначения

- выключатель одноклавишный
- выключатель двухклавишный (флажков — по числу клавиш)
- выключатель с проходной или перекрёстной клавишей (обратный флажок); тип клавиши — в подписи
- S1 → марка → группы по клавишам (через «;»): прох. — проходной, перекр. перекрёстный, дим. светорегулятор; H — высота
- связь: выключатель → ближайший светильник группы в том же помещении (не трасса кабеля); полный состав группы — по номеру L
- светильник встраиваемый точечный
- светильник потолочный накладной
- светильник подвесной
- светильник настенный (бра), H высота оси
- линейный светильник настенный (подсветка столешницы), точка вывод питания
- светодиодная лента в профиле / в карнизе короба
- трековая система
- L1 группа включения у светильника
- стояк: К1 — канализация, В1 — ХВС, Т3 — ГВС
- 1 номер помещения, площадь м²

Допущения и предложения на листе

Основа листа: размеры сняты с растрового плана заказчика без размеров: масштаб восстановлен по площадям помещений (≈ 11,8 мм на пиксель), контрольный обмер не выполнен (К-1); высота потолка 2700 мм принята: на плане заказчика её нет (К-2); толщины стен 300 / 120 мм приняты по плану заказчика, не замерены (К-1); разрешённая мощность 15 кВт принята по типовым ТУ для квартиры, ТУ заказчиком не переданы (К-4); подрайон климата не задан — принят не северный (жилые от 2,5 м) (К-9).

Открытые вопросы и конфликты по листу: К-13, К-14.

См. лист открытых вопросов (лист 6, записи К-1, К-2, К-4; лист 7, записи К-9, К-13, К-14).

Примечания

1. За отметку 0,000 принят уровень чистого пола. Высоты H — от чистого пола до оси изделия; привязки — от чистовой грани стены до оси механизма (у рамки на несколько постов — до оси рамки).
2. Высота установки, не указанная на плане: выключатели — 900 мм от чистого пола (у кровати и другие — H у марки), со стороны дверной ручки (ПУЭ 7.1.51).
3. Какой выключатель какие светильники включает — по номеру группы L: у выключателя (S1 → L1; L2 — клавиши по порядку) и у каждого светильника. Пунктир подсказка к ближайшему светильнику группы в том же помещении (не дальше 3 м), это не трасса кабеля; выключатель за стеной (у двери санузла) и далёкая группа — только номер группы.
4. Группы из нескольких мест (L8 — S4, S6; L3 — S3, S5; L7 — S4, S7, S8; L9 — S7, S8): на крайних местах — проходные клавиши, на промежуточных — перекрёстные; механизмы — в ведомости изделий.
5. Вентиляторы санузлов (выводы ЭВ на плане розеток) включаются вместе с основным светом помещения, отключаются с задержкой — таймер выбега в вентиляторе.
6. Розеточные и мокрые линии — через УЗО или дифавтомат с током утечки не более 30 мА (ПУЭ 7.1.79); в санузле выполнить ДСУП (ПУЭ 7.1.87–7.1.88).
7. Кабель — медный, исполнение нг(А)-LS (ГОСТ 31565-2012); скрытая прокладка только горизонтально и вертикально, фактические трассы зафиксировать исполнительной схемой до закрытия отделкой.
8. Расчёт нагрузок, токов КЗ, селективности и сечений — по проекту ЭОМ организации с допуском СРО; лист задаёт состав, расположение и группы.
9. Группы без выключателя: L4 — выключатель в исходных данных не задан; управление группой согласуется до монтажа.
10. Расшифровка клавиш и ведомость изделий — лист 32.

1000 мм · печать 1:1

						ГД-2026-007-АИ
						Квартира 65 м²
						Общая площадь 65,24* м² · * размеры со скана, не замерены (реестр — л. 6–8, К-1)
Изм.	Кол.уч	Лист	№ док.	Подп.	Дата	
Разраб.		Кырлан А.С.			14.11.26	Дизайн-проект интерьера
Пров.						Стадия: РП · Лист: 31 · Листов: 117
ГИП						
Н. контр.						**План выключателей и схема включения** · М 1:50
Утв.						**Кырлан Александр Сергеевич**

выпуск 14.11.2026 № 9cc0b98f36 · стр. 34 из 139

Ведомость электроточек и изделий

Электроточки, изделия, светильники, освещённость, клавиши выключателей · б/м

Ведомость электроточек

Марка	Пом.	Назначение	Н, мм	Гр.
Р1	2	розетка общего назначения	600	4
Р2	2	розетка общего назначения	600	4
Р3	2	комод, зарядка	300	4
Р4	3	ТВ, приставка	1100	4
Р5	3	обеденная зона	300	4
Р6	3	торшер у кресла М3**	300	4
Р7	3	у дивана	300	4
Р8	3	у дивана	300	4
Р15	3	холодильник	300	2
Р16	3	рабочая зона	1100	2
Р17	3	рабочая зона	1100	2
Р18	3	рабочее место	900	4
ЭВ1	3	варочная панель	150	3
ЩК	4	щит квартирный	1700	
Р19	5	уборка	300	4
ЭВ4**	6	вентилятор ВР2 (таймер выбега)	2400	1
КУП1	7	КУП	300	
Р20	7	фен, IP44	1100	5
Р21	7	стиральная машина, IP44	1100	5
ЭВ2	7	вентилятор (клавиша L4, таймер выбега)	2400	1
ЭВ3	7	полотенцесушитель, IP44	1000	5
Р9	9	у кровати	600	5
Р10	9	у кровати	600	5
Р11	9	торшер у кровати С6 (изголовье)	300	5
Р12**	9	ТВ (в одной зоне с ТВ2, LAN4 на стене А)	1100	5
Р13	9	уборка	300	5
Р14	9	уборка у входа	300	5

Ведомость изделий

Наименование	Марки	Ед.	Кол.
Розетка с з/к и защитными шторками, 16 А	по ведомости точек	шт	22
Розетка IP44 с крышкой, 16 А	Р20, Р21	шт	2
Выключатель 1-клав.	S2	шт	1
Выключатель 1-клав. проходной	S3, S5, S6	шт	3
Выключатель 2-клав.	S1	шт	1
Выключатель 2-клав. (перекрёстная + проходная)	S7	шт	1
Выключатель 2-клав. проходной	S4, S8	шт	2
Рамка 1-постовая	в т. ч. 8 под выключ.	шт	26
Рамка 2-постовая		шт	3
Коробка установочная (подрозетник) Ø68	розетки, выключатели	шт	32
Вывод кабеля под прибор (клеммник)	ЭВ1–ЭВ3	шт	3
Вывод кабеля к вентилятору вытяжки	ЭВ4**	шт	1
Коробка уравнивания потенциалов КУП	КУП1	шт	1
Блок питания LED 24 В, 60 Вт	БП1, БП2	шт	2
Блок питания LED 24 В, 200 Вт, дим.	БП3	шт	1
Извещатель дымовой автономный	ИП1, ИП2, ИП5	шт	3
Извещатель тепловой	ИП3**, ИП4**	шт	2
Щит квартирный (состав — лист щита)	ЩК	шт	1
Розетка компьютерная RJ45, кат. 6, с рамкой и подрозетником	LAN1–LAN4	шт	4
Розетка телевизионная (коаксиальная) с рамкой и подрозетником	ТВ1, ТВ2	шт	2
Трубка или монитор домофона (поставка домофонной организации)	ДФ1	шт	1
Щит слаботочный ЩС**: корпус, DIN-рейка, розетки 220 В	ЩС**	шт	1
Патч-панель, портов не менее 4		шт	1
Коммутатор, портов не менее 4, из них PoE 0		шт	1
Кабель домофона — тип по системе поставщика (по лучам от ЩС**, запас 10 %)		м	3,1

Ведомость изделий (продолжение)

Наименование	Марки	Ед.	Кол.
Кабель коаксиальный RG-6 (75 Ом) к розеткам ТВ (по лучам от ЩС**, запас 10 %)		м	30,2
Кабель U/UTP кат. 5e (LAN, Wi-Fi и камеры по PoE) (по лучам от ЩС**, запас 10 %)		м	42,7
Кабель U/UTP кат. 6 (LAN, Wi-Fi и камеры по PoE) (по лучам от ЩС**, запас 10 %)		м	14,2

Ведомость светильников

Поз.	Марки	Тип	Кол.	Р, Вт	Ф, лм	IP	Тц/Ra
1	Св16	потолочный накладной	1	10	900		3000/90
2	Св1	потолочный накладной	1	36	3200		2700/90
3	Св5**	трековая система	2	12	900		2700/90
4	Св2, Св3	настенный (бра), Н=1300	2	4	250		2700/90
5	Св4	подвесной	1	24	2400		3000/90
6	Св6	потолочный накладной	1	18	1800		3000/90
7	Св7	потолочный накладной	1	12	1100		3000/90
8	Св8	потолочный накладной	1	12	1000		4000/90
9	Св9	линейный светильник, Н=1400	1	18	1300		3000/90
10	Св10–Св12	встраиваемый точечный	3	9	800		3000/90
11	Св13	встраиваемый точечный	1	6	500		3000/90
12	Св14	встраиваемый точечный	1	9	700	44	3000/90
13	Св15	настенный (бра), Н=1900	1	6	400	44	3000/90
14	Св26	потолочный накладной	1	9	600		3000/90
15	Св17–Св22	встраиваемый точечный	6	12	1050		2700/90
16	Св23	светодиодная лента, 13,8 м	1	132,5	12420		2700/90
17	Св24, Св25	настенный (бра), Н=1500	2	6	400		2700/90

Освещённость (оценка)

Пом.	S, м²	Ен, лк	Ф треб., лм	Ф по пр., лм
1	4,2	75	890	900
2	8,3	150	3490	5000
3	18,9	150	7990	6300
4	4,2	50	580	800
5	5,5	50	780	1600
6	1,8	50	260	500
7	3,9	50	540	700
8	2,5	30	210	600
9	16	200	9030	6300

Расшифровка клавиш

Марка	Пом.	Н, мм	Клав.	Механизм	Группа: светильники
S1	3	900	1	обычный	L1: Св4, Св6–Св8
			2	обычный	L6: Св9, Св16
S2	2	900	1	обычный	L2: Св1, Св5**
S3	4	900	1	проходной	L3: Св10–Св12, Св26
S4	9	900	1	проходной	L7: Св17–Св22
			2	проходной	L8: Св2, Св3, Св23
S5	5	900	1	проходной	L3: Св10–Св12, Св26
S6	2	900	1	проходной	L8: Св2, Св3, Св23
S7	9	800	1	перекрёстный	L7: Св17–Св22
			2	проходной	L9: Св24, Св25
S8	9	800	1	проходной	L7: Св17–Св22
			2	проходной	L9: Св24, Св25

Допущения и предложения на листе. Основа листа: размеры сняты с растрового плана заказчика без размеров: масштаб восстановлен по площадям помещений (≈ 11,8 мм на пиксель), контрольный обмер не выполнен (К-1); высота потолка 2700 мм принята: на плане заказчика её нет (К-2); толщины стен 300 / 120 мм приняты по плану заказчика, не замерены (К-1); разрешённая мощность 15 кВт принята по типовым ТУ для квартиры, ТУ заказчиком не переданы (К-4); подрайон климата не задан — принят не северный (жилые от 2,5 м) (К-9). Знак «**» — предложение проектировщика, заказчиком не утверждено (согласовать с заказчиком): Св5 — трековая система 2 × 900 лм: светильник добавлен проектировщиком, поток принят до нормы освещённости, модель и паспорт не выбраны; ИП3, ИП4 — прихожая / кухня квартиры — тепловой (СП 484, прил. Б, Б.4); место — центр помещения, не ближе 500 мм к светильнику; Р12 — Было: стена В смещение 1985, назначение «ТВ над комодом» — над кроватью С6, ТВ2 и LAN4 при этом на стене А, комода в помещении нет (назначение по шаблону); ЭВ4 — вывод к бытовому вентилятору, таймер выбега; ЩС — щит слаботочный: место и состав; К-5: М3 — Было х 800, у 1750 — место занял диван М1. См. лист открытых вопросов (лист 6, записи К-1, К-2, К-4, К-5; лист 7, запись К-9).

Примечания

1. Ведомости сведены с планов розеток, освещения и выключателей; марки, группы и высоты — те же, что у знаков на планах.
2. Механизмы, рамки и светорегуляторы — одной серии; число постов и клавиш сверено с выбранной серией. Перекрёстная клавиша — отдельный механизм серии.
3. Освещённость (оценка) — по норме СанПиН 1.2.3685-21 (табл. 5.52, на полу), не светотехнический расчёт; декоративная подсветка в оценку не входит.
4. За отметку 0,000 принят уровень чистого пола. Высоты Н — от чистого пола до оси изделия; привязки — от чистовой грани стены до оси механизма (у рамки на несколько постов — до оси рамки).
5. Розеточные и мокрые линии — через УЗО или дифавтомат с током утечки не более 30 мА (ПУЭ 7.1.79); в санузле выполнить ДСУП (ПУЭ 7.1.87–7.1.88).
6. Кабель — медный, исполнение нг(А)-LS (ГОСТ 31565-2012); скрытая прокладка только горизонтально и вертикально, фактические трассы зафиксировать исполнительной схемой до закрытия отделкой.
7. Расчёт нагрузок, токов КЗ, селективности и сечений — по проекту ЭОМ организации с допуском СРО; лист задаёт состав, расположение и группы.

Изм.	Кол.уч	Лист	№ док.	Подп.	Дата
Разраб.		Кырлан А.С.			14.11.26
Пров.					
ГИП					
Н. контр.					
Утв.					

ГД-2026-007-АИ

Квартира 65 м²

Общая площадь 65,24* м² · * размеры со скана, не замерены (реестр — л. 6–8, К-1)

Дизайн-проект интерьера

Стадия	Лист	Листов
РП	32	117

Ведомость электроточек и изделий


М б/м

Кырлан Александр Сергеевич

выпуск 14.11.2026 № 9cc0b98f36 · стр. 35 из 139

Однолинейная схема щита

Щит квартирный ЩК · без масштаба

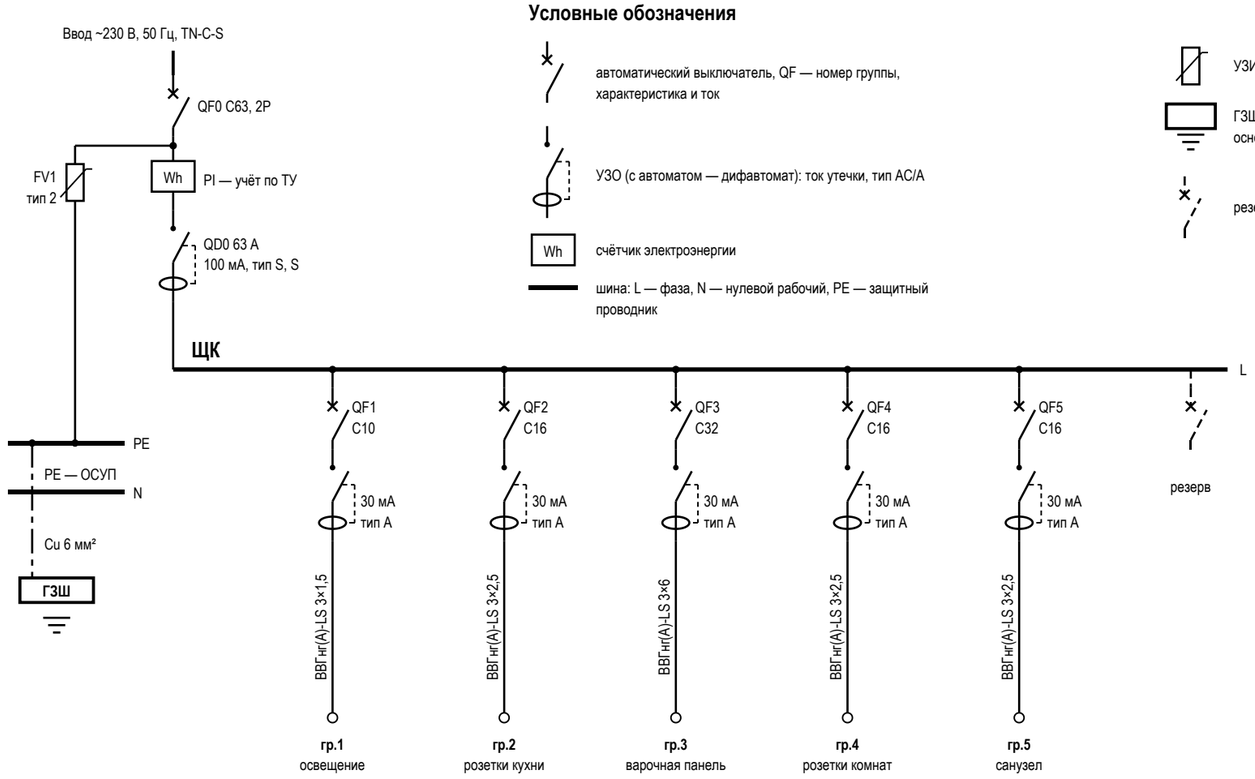

Условные обозначения

- автоматический выключатель, QF — номер группы, характеристика и ток
- УЗО (с автоматом — дифавтомат): ток утечки, тип AC/A
- Wh — счётчик электроэнергии
- шина: L — фаза, N — нулевой рабочий, PE — защитный проводник
- УЗИП (ограничитель перенапряжений), FV — марка
- ГЗШ — главная заземляющая шина; штрихпунктир — проводник основной системы уравнивания потенциалов (ОСУП)
- резервный аппарат (не менее 20 % групп)

Данные щитка

Показатель	Значение
Номер щитка	ЩК
Тип	ЩРВ-П-24, IP41
Уст. мощность, кВт	
Разреш. мощность, кВт	15
Расчётная, кВт	9,8
Автоматы 1п: занят. / рез.	5 / 1
Модулей: всего / занято	24 / 16
Ток на вводе, А	63
Вводной аппарат	QF0 C63, 2P
УЗИП	FV1, тип 2, ЩК, после счётчика
ГЗШ, проводник ОСУП	Cu 6 мм²

Таблица групп щита ЩК и кабельный журнал

№	Назначение	Помещения	Автомат	УЗО / дифавтомат	Кабель	Длина, м	Р, кВт	Точек
1	освещение	1, 2, 3, 4, 5, 6, 7, 8, 9	C10	30 мА, тип A	ВВГнг(A)-LS 3×1,5	140,7		38
2	розетки кухни	3	C16	30 мА, тип A	ВВГнг(A)-LS 3×2,5	20,4		3
3	варочная панель	3	C32	30 мА, тип A	ВВГнг(A)-LS 3×6	17,2		1
4	розетки комнат	2, 3, 5	C16	30 мА, тип A	ВВГнг(A)-LS 3×2,5	52,4		10
5	санузел	7, 9	C16	30 мА, тип A	ВВГнг(A)-LS 3×2,5	47,1		9
	Итого по сечениям ВВГнг(A)-LS, м: 3×1,5 — 140,7; 3×2,5 — 119,9; 3×6 — 17,2					277,8		

Примечания

1. Схема однолинейная: одна линия — фаза, N и PE группы; аппараты — в отключённом положении (ГОСТ 2.702, ГОСТ 2.755). Номера групп — как у точек на планах (гр.). За отметку 0,000 принят уровень чистого пола; высота щита — по плану розеток.
2. Розеточные и мокрые линии — через УЗО или дифавтомат с током утечки не более 30 мА (ПУЭ 7.1.79); в санузле выполнить ДСУП (ПУЭ 7.1.87–7.1.88).
3. УЗО тип A — для линий с электроникой, стиральной и посудомоечной машиной, LED-драйверами; тип AC — только для чисто активной нагрузки.
4. Кабель — медный, исполнение нг(A)-LS (ГОСТ 31565-2012); скрытая прокладка только горизонтально и вертикально, фактические трассы зафиксировать исполнительной схемой до закрытия отделкой.
5. Номинал автомата — не выше допустимого тока кабеля: 1,5 мм² — до 10 А, 2,5 мм² — до 16 А. Резерв щита — не менее 20 % модулей.
6. Расчёт нагрузок, токов КЗ, селективности и сечений — по проекту ЭОМ организации с допуском СРО; лист задаёт состав, расположение и группы.
7. УЗИП FV1 — после вводного автомата, проводник к шине PE — кратчайший, без петель. Шина PE щита соединяется с ГЗШ проводником ОСУП; к ГЗШ присоединяются трубы водопровода и отопления на вводе в квартиру (ПУЭ 7.1.87). Шины N и PE — раздельные, после разделения PEN не объединяются.
8. До подключения нагрузки — приёмо-сдаточные испытания с протоколом: сопротивление изоляции линий не менее 0,5 МОм, срабатывание УЗО по току и времени, непрерывность защитных проводников PE (ПУЭ, гл. 1.8).

Допущения и предложения на листе

Основа листа: размеры сняты с растрового плана заказчика без размеров: масштаб восстановлен по площадям помещений (≈ 11,8 мм на пиксель), контрольный обмер не выполнен (К-1); высота потолка 2700 мм принята: на плане заказчика её нет (К-2); толщины стен 300 / 120 мм приняты по плану заказчика, не замерены (К-1); разрешённая мощность 15 кВт принята по типовым ТУ для квартиры, ТУ заказчиком не переданы (К-4); подрайон климата не задан — принят не северный (жилые от 2,5 м) (К-9).

Открытые вопросы и конфликты по листу: К-4.

См. лист открытых вопросов (лист 6, записи К-1, К-2, К-4; лист 7, запись К-9).

Изм.	Кол.уч	Лист	№ док.	Подп.	Дата
Разраб.		Кырлан А.С.			14.11.26
Пров.					
ГИП					
Н. контр.					
Утв.					

ГД-2026-007-АИ

Квартира 65 м²

Общая площадь 65,24* м² · * размеры со скана, не замерены (реестр — л. 6–8, К-1)

Дизайн-проект интерьера

Стадия	Лист	Листов
РП	33	117

Однолинейная схема щита

М б/м


Кырлан Александр Сергеевич

План принципиальных трасс

Силовые трассы и объёмы электромонтажа, слаботочка в объёмах · размеры в мм

ПРЕДВАРИТЕЛЬНО · не для производства работ · открыто пунктов: 14 (реестр — л. 6–8)

План принципиальных трасс (М 1:100)

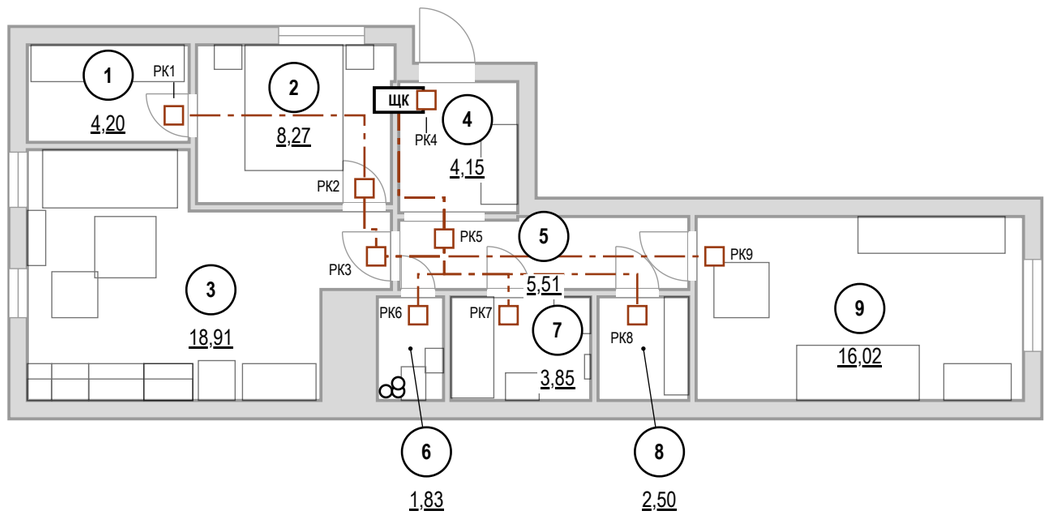

Кабель по группам ВВГнг(А)-LS, м

Гр.	мм²	Трасса	Данные
1	3×1,5	140,7	
2	3×2,5	20,4	
3	3×6	17,2	

Гр.	мм²	Трасса	Данные
4	3×2,5	52,4	
5	3×2,5	47,1	
Σ		**277,8**	

Экспликация помещений

№	Помещение	Площадь, м²
1	Гардеробная	4,20
2	Спальня	8,27
3	Кухня-гостиная	18,91
4	Прихожая	4,15
5	Коридор	5,51
6	Санузел	1,83
7	Ванная	3,85
8	Кладовая	2,50
9	Детская	16,02
	Итого (общая площадь)	65,24

Объёмы прокладки

Работа, материал	Ед.	Кол.
Гофротруба Ø20 в потолочном пространстве	м	97,8
Кабель-канал плинтуса для силовых линий	м	83,3
Короб или накладной канал для вертикальных спусков и подъёмов	м	51
Коробка распределительная (РК) над дверью помещения	шт	9
Слаботочка: кабель домофона	м	3,1
Слаботочка: Кабель коаксиальный RG-6 (75 Ом) к розеткам ТВ	м	30,2
Слаботочка: Кабель U/UTP кат. 5е (LAN, Wi-Fi и камеры по PoE)	м	42,7
Слаботочка: U/UTP кат. 6 (LAN, Wi-Fi, камеры)	м	14,2
Слаботочка: гофротруба Ø20 отдельно от силовых	м	81,2

Штробы — только после заключения

Работа	Ед.	Кол.
Вертикальные штробы 20×20 мм от потолка до каждой настенной точки (в маршрут без штроб не входят)	м	69,81

Условные обозначения

- **ЩК** — щит квартирный
- РК — распределительная коробка над дверью помещения
- магистраль от щита к РК: потолочное пространство, гофра
- мебель и сантехприборы — подложка

Допущения и предложения на листе

Основа листа: размеры сняты с растрового плана заказчика без размеров: масштаб восстановлен по площадям помещений (≈ 11,8 мм на пиксель), контрольный обмер не выполнен (К-1); высота потолка 2700 мм принята: на плане заказчика её нет (К-2); толщины стен 300 / 120 мм приняты по плану заказчика, не замерены (К-1); разрешённая мощность 15 кВт принята по типовым ТУ для квартиры, ТУ заказчиком не переданы (К-4); подрайон климата не задан — принят не северный (жилые от 2,5 м) (К-9).
Знак «**» — предложение проектировщика, заказчиком не утверждено (согласовать с заказчиком): ЩС — щит слаботочный: место и состав.
См. лист открытых вопросов (лист 6, записи К-1, К-2, К-4; лист 7, запись К-9).

Примечания

1. За отметку 0,000 принят уровень чистого пола. Высоты Н — от чистого пола до оси изделия; привязки — от чистовой грани стены до оси механизма (у рамки на несколько постов — до оси рамки).
2. Розеточные и мокрые линии — через УЗО или дифавтомат с током утечки не более 30 мА (ПУЭ 7.1.79); в санузле выполнить ДСУП (ПУЭ 7.1.87–7.1.88).
3. Кабель — медный, исполнение нг(А)-LS (ГОСТ 31565-2012); скрытая прокладка только горизонтально и вертикально, фактические трассы зафиксировать исполнительной схемой до закрытия отделкой.
4. Расчёт нагрузок, токов КЗ, селективности и сечений — по проекту ЭОМ организации с допуском СРО; лист задаёт состав, расположение и группы.
5. Длины — по плану: от щита вверх в потолочное пространство, по дверям и коридору без захода в мокрые помещения к распределительной коробке над дверью, далее к точкам; вертикали считаются вниз и обратно (у последней точки цепочки — в один конец); запас 10 %. Трассы принципиальные: фактическую зафиксировать исполнительной схемой до закрытия отделкой.
6. Несущие стены не определены: штробы в стенах не выполнять. Маршрут проложен без штроб: горизонтали — за потолком в гофре (97,8 м) и в кабель-канале плинтуса (83,3 м), вертикали — в коробе или накладном канале (89,7 м кабеля). Точек: за потолком — 21, спуск из потолка — 8, по плинтусу — 11, плинтус и подъём — 22.
7. Вариант со штробами — работа после технического заключения: 69,81 м вертикальных штроб от потолка до каждой настенной точки; условие — только после технического заключения: стена не несущая (или вертикальная штроба в несущей согласована конструктором), глубина и ширина 20–25 мм, не в зонах 0–2 ванной. Без заключения и согласования конструктора в смету и в график эта работа не входит.
8. Слаботочные сети: кабели и точки считаются по лучам от ЩС** (лист слаботочных сетей): 90 м, портов патч-панели и коммутатора не менее 4. Изделия — в ведомости изделий.

1000 мм · печать 1:1

Изм.	Кол.уч	Лист	№ док.	Подп.	Дата	ГД-2026-007-АИ			
						Квартира 65 м²			
						Общая площадь 65,24* м² · * размеры со скана, не замерены (реестр — л. 6–8, К-1)			
Разраб.		Кырлан А.С.			14.11.26	Дизайн-проект интерьера	Стадия	Лист	Листов
Пров.							РП	34	117
ГИП						План принципиальных трасс	Кырлан Александр Сергеевич		
						М 1:100			
Н. контр.									
Утв.									

выпуск 14.11.2026 № 9cc0b98f36 · стр. 37 из 139

Таблица нагрузок щита

щит ЩК · 5 групп · Ррасч 0 кВт · без масштаба

Группы щита ЩК (1)

№	Назначение	Руст, кВт	Кс	Ррасч, кВт	Iрасч, А	Автомат	Кабель
1	освещение	0	0,6	0	0	C10	3×1,5
2	розетки кухни	0	0,4	0	0	C16	3×2,5
3	варочная панель	0	0,6	0	0	C32	3×6

Группы щита ЩК (2)

№	Назначение	Руст, кВт	Кс	Ррасч, кВт	Iрасч, А	Автомат	Кабель
4	розетки комнат	0	0,4	0	0	C16	3×2,5
5	санузел	0	0,7	0	0	C16	3×2,5

Итог по квартире

Показатель	Значение
Установленная мощность Σ Руст	0 кВт
Σ Руст × Кс по группам	0 кВт
Коэффициент одновременности	0,7
Расчётная мощность квартиры Ррасч	0 кВт
Расчётный ток Iрасч (230 В, cosφ 0,95)	0 А
Разрешённая мощность	15 кВт
Запас до разрешённой	100 %
Вводной аппарат	C63, 2P

Примечания

1. Руст — установленная мощность группы по данным щита (приборы — по паспорту, розетки общего назначения — оценка 0,1 кВт на гнездо). Кс — коэффициенты спроса: освещение 0,6; розетки 0,4; варочная и духовой 0,6; кондиционеры 0,8; тёплый пол 1,0; прочие 0,7; одновременность 0,7.
2. Коэффициенты — ориентир исполнителя, не табличные значения нормы; расчёт нагрузки подтверждает инженер ЭОМ (СП 256.1325800.2016). Под разрешённую мощность они не подгоняются.
3. Вывод: запас 100 % (расчётная 0 кВт при разрешённой 15 кВт).
4. Розеточные и мокрые линии — через УЗО или дифавтомат с током утечки не более 30 мА (ПУЭ 7.1.79); в санузле выполнить ДСУП (ПУЭ 7.1.87–7.1.88).

Допущения и предложения на листе

Основа листа: размеры сняты с растрового плана заказчика без размеров: масштаб восстановлен по площадям помещений (≈ 11,8 мм на пиксель), контрольный обмер не выполнен (К-1); высота потолка 2700 мм принята: на плане заказчика её нет (К-2); толщины стен 300 / 120 мм приняты по плану заказчика, не замерены (К-1); разрешённая мощность 15 кВт принята по типовым ТУ для квартиры, ТУ заказчиком не переданы (К-4); подрайон климата не задан — принят не северный (жилые от 2,5 м) (К-9).
См. лист открытых вопросов (лист 6, записи К-1, К-2, К-4; лист 7, запись К-9).

Изм.	Кол.уч	Лист	№ док.	Подп.	Дата
Разраб.		Кырлан А.С.			14.11.26
Пров.					
ГИП					
Н. контр.					
Утв.					

ГД-2026-007-АИ

Квартира 65 м²

Общая площадь 65,24* м² · * размеры со скана, не замерены (реестр — л. 6–8, К-1)

Дизайн-проект интерьера

Стадия	Лист	Листов
РП	35	117

Таблица нагрузок щита

М б/м


Кырлан Александр Сергеевич

выпуск 14.11.2026 № 9cc0b98f36 · стр. 38 из 139

План слаботочных сетей

Интернет, ТВ, домофон · размеры в мм · высоты от чистого пола

План слаботочных сетей (М 1:75)

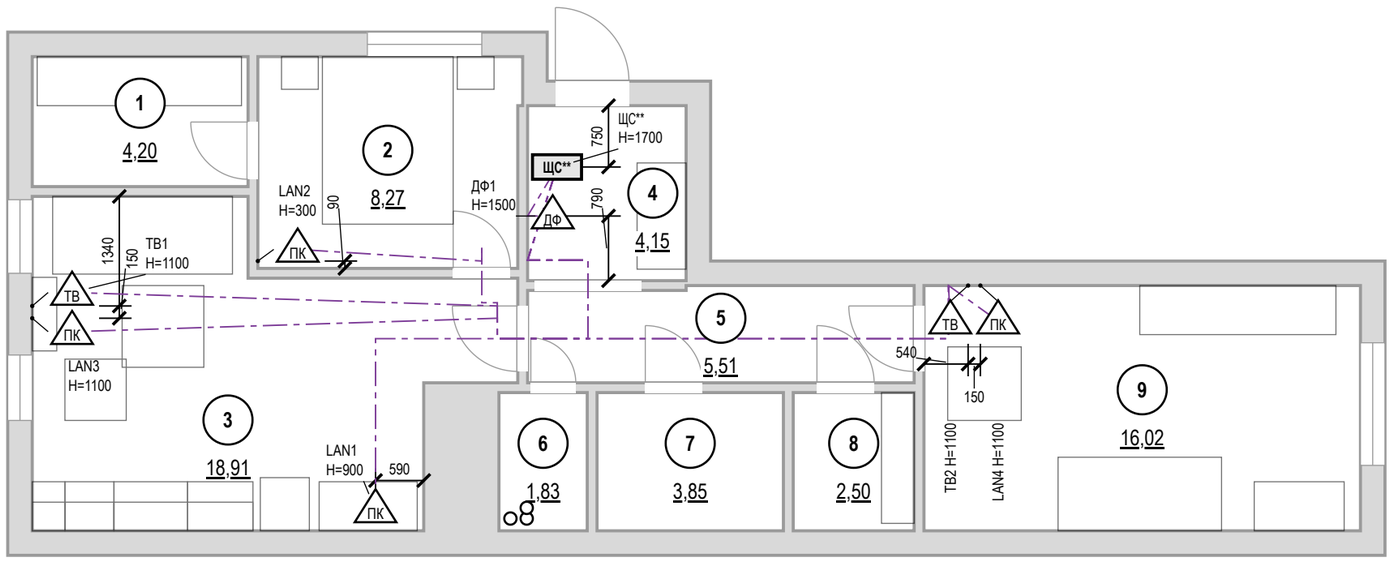

ПРЕДВАРИТЕЛЬНО · не для производства работ · открыто пунктов: 14 (реестр — л. 6–8)

Ведомость слаботочных точек

Марка	Пом.	Назначение	H, мм	Кабель
LAN2	2	розетка LAN (RJ45)	300	U/UTP кат. 5e/6
ТВ1	3	розетка ТВ	1100	RG-6 (75 Ом)
LAN3	3	розетка LAN (RJ45)	1100	U/UTP кат. 5e/6
LAN1	3	розетка LAN (RJ45)	900	U/UTP кат. 5e/6
ДФ1	4	домофон (трубка)	1500	по системе
ТВ2	9	розетка ТВ	1100	RG-6
LAN4	9	розетка LAN (RJ45)	1100	U/UTP кат. 6
ЩС**	4	щит слаботочный	1700	ввод пров.

Условные обозначения

- ЩС — щит слаботочный: ввод провайдера, роутер, коммутатор
- ПК — розетка компьютерная RJ45
- ТВ — розетка телевизионная
- ДФ — трубка или монитор домофона
- кабель от ЩС до точки, отдельным лучом
- мебель и сантехприборы — подложка
- стояк: К1 — канализация, В1 — ХВС, Т3 — ГВС
- 1 — номер помещения, площадь м²

Допущения и предложения на листе

Основа листа: размеры сняты с растрового плана заказчика без размеров: масштаб восстановлен по площадям помещений (≈ 11,8 мм на пиксель), контрольный обмер не выполнен (К-1); высота потолка 2700 мм принята: на плане заказчика её нет (К-2); толщины стен 300 / 120 мм приняты по плану заказчика, не замерены (К-1); разрешённая мощность 15 кВт принята по типовым ТУ для квартиры, ТУ заказчиком не переданы (К-4); подрайон климата не задан — принят не северный (жилые от 2,5 м) (К-9).

Знак «**» — предложение проектировщика, заказчиком не утверждено (согласовать с заказчиком): ЩС — щит слаботочный: место и состав.

См. лист открытых вопросов (лист 6, записи К-1, К-2, К-4; лист 7, запись К-9).

Примечания

1. За отметку 0,000 принят уровень чистого пола. Высоты H — от чистого пола до оси изделия; привязки — от чистовой грани стены до оси механизма (у рамки на несколько постов — до оси рамки).
2. Высота установки, не указанная на плане: розетки LAN и ТВ — 300 мм от чистого пола.
3. Слаботочные кабели — отдельно от силовых: в своей трубе или лотке, при параллельной прокладке не ближе 100 мм к силовым, пересечения под прямым углом; каждую точку — отдельным кабелем от ЩС** без скруток.
4. Трассы на листе — принципиальные; фактические зафиксировать исполнительной схемой до закрытия отделкой. Силовые линии, УЗО 30 мА, ДСУП, кабель нг(А)-LS — по листам розеток и щита.
5. Проект силовой части и расчёт токов КЗ — по проекту ЭОМ; слаботочная часть согласуется с провайдером и управляющей компанией (домофон, коллективное ТВ).

1000 мм · печать 1:1

Изм.	Кол.уч	Лист	№ док.	Подп.	Дата
Разраб.		Кырлан А.С.			14.11.26
Пров.					
ГИП					
Н. контр.					
Утв.					

ГД-2026-007-АИ

Квартира 65 м²

Общая площадь 65,24* м² · * размеры со скана, не замерены (реестр — л. 6–8, К-1)

Дизайн-проект интерьера

Стадия	Лист	Листов
РП	36	117

План слаботочных сетей

М 1:75

Кырлан Александр Сергеевич

выпуск 14.11.2026 № 9cc0b98f36 · стр. 39 из 139

04

Отопление и вентиляция

Кырлан Александр Сергеевич


выпуск 14.11.2026 · 9cc0b98f36 · стр. 40 из 139

План вентиляции

Вытяжка, приток, переток · кондиционирование не предусмотрено · размеры в мм · высоты от чистого пола

ПРЕДВАРИТЕЛЬНО · не для производства работ · открыто пунктов: 14 (реестр — л. 6–8)

План вентиляции (М 1:50)

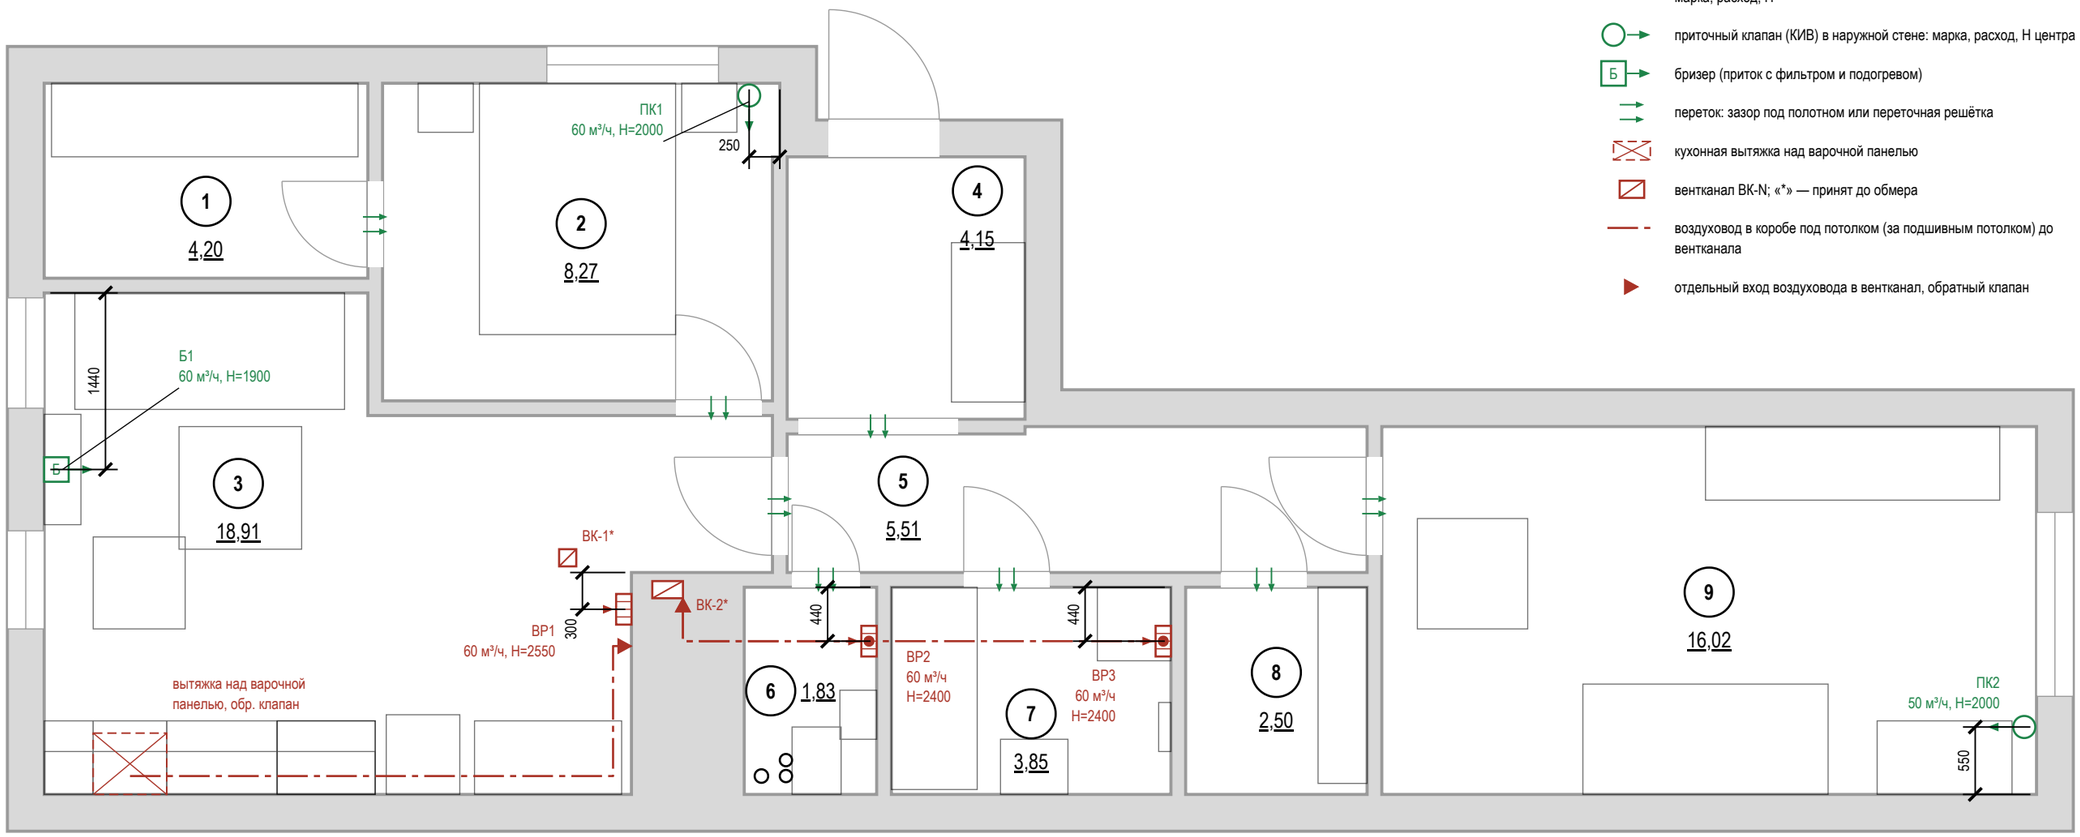

Условные обозначения

- стояк: К1 — канализация, В1 — ХВС, Т3 — ГВС
- номер помещения, площадь м²
- вытяжная решётка в вентканал: марка, расход м³/ч, H центра от чистого пола
- вытяжная решётка с бытовым вентилятором и обратным клапаном: марка, расход, H
- приточный клапан (КИВ) в наружной стене: марка, расход, H центра
- Б — бризер (приток с фильтром и подогревом)
- переток: зазор под полотном или переточная решётка
- кухонная вытяжка над варочной панелью
- вентканал ВК-N; «*» — принят до обмера
- воздуховод в коробе под потолком (за подшивным потолком) до вентканала
- отдельный вход воздуховода в вентканал, обратный клапан

Примечания

1. Расчёт систем ОВ и подбор оборудования — проектная организация с допуском СРО; лист даёт места, трассы и привязки.
2. Нормы вытяжки — СП 54.13330.2022 (Изм. 1, 2), табл. 7.1: кухня с электроплитой 60 м³/ч, с газовой 100; ванная и совмещённый санузел 50; уборная 25; гардеробная 0,2 ч⁻¹. Приток в жилые — 3 м³/ч на 1 м² (менее 20 м² общей площади на человека), иначе 30 м³/ч на человека.
3. Вентканалы и шахты не сужать, не переносить и не закрывать; вентилятор и кухонная вытяжка — через обратный клапан, без перекрытия естественной тяги; ВР2 — воздуховодом до ВК-2 ≈ 1,9 м, ВР3 — воздуховодом до ВК-2 ≈ 4,3 м в коробе под потолком.
4. Проектные расходы — не ниже нормы, вытяжка сведена с притоком вентиляторами мокрых помещений. Клапаны — в простенке у окна, центр 2000 мм, не над кроватью, не ближе 300 мм к стоякам отопления; типоразмер — на расход.
5. Кухонная вытяжка в воздухообмен не включена: воздуховод не менее Ø125 в коробе, вход в канал отдельный.
6. Переток — зазор под полотнами межкомнатных дверей или переточная решётка.
7. Кондиционирование заданием не предусмотрено; при установке трассы фреона и дренажа (не менее 40 мм/м, в К1 через сифон) и питание заложить до черновых работ.
8. Привязки оборудования — по паспортам приобретённых моделей, до черновых работ.
9. Привязки — до обмера: вентканалы ВК-N* приняты проектировщиком, решётки и воздуховоды — от них. До черновых работ — обмер каналов и тяги, лист перевыпустить по факту.

Допущения и предложения на листе

Основа листа: размеры сняты с растрового плана заказчика без размеров: масштаб восстановлен по площадям помещений (≈ 11,8 мм на пиксель), контрольный обмер не выполнен (К-1); высота потолка 2700 мм принята: на плане заказчика её нет (К-2); толщины стен 300 / 120 мм приняты по плану заказчика, не замерены (К-1); разрешённая мощность 15 кВт принята по типовым ТУ для квартиры, ТУ заказчиком не переданы (К-4); подрайон климата не задан — принят не северный (жилые от 2,5 м) (К-9).

Открытые вопросы и конфликты по листу: К-6, К-7.

См. лист открытых вопросов (лист 6, записи К-1, К-2, К-4, К-6, К-7; лист 7, запись К-9).

1000 мм · печать 1:1

Изм.	Кол.уч	Лист	№ док.	Подп.	Дата
Разраб.		Кырлан А.С.			14.11.26
Пров.					
ГИП					
Н. контр.					
Утв.					

ГД-2026-007-АИ

Квартира 65 м²

Общая площадь 65,24* м² · * размеры со скана, не замерены (реестр — л. 6–8, К-1)

Дизайн-проект интерьера

Стадия	Лист	Листов
РП	37	117

План вентиляции

М 1:50

Кырлан Александр Сергеевич


выпуск 14.11.2026 № 9cc0b98f36 · стр. 41 из 139

План отопления

Радиаторы, стояки, подводки · размеры в мм · высоты от чистого пола

План отопления (М 1:50)

ПРЕДВАРИТЕЛЬНО · не для производства работ · открыто пунктов: 14 (реестр — л. 6–8)

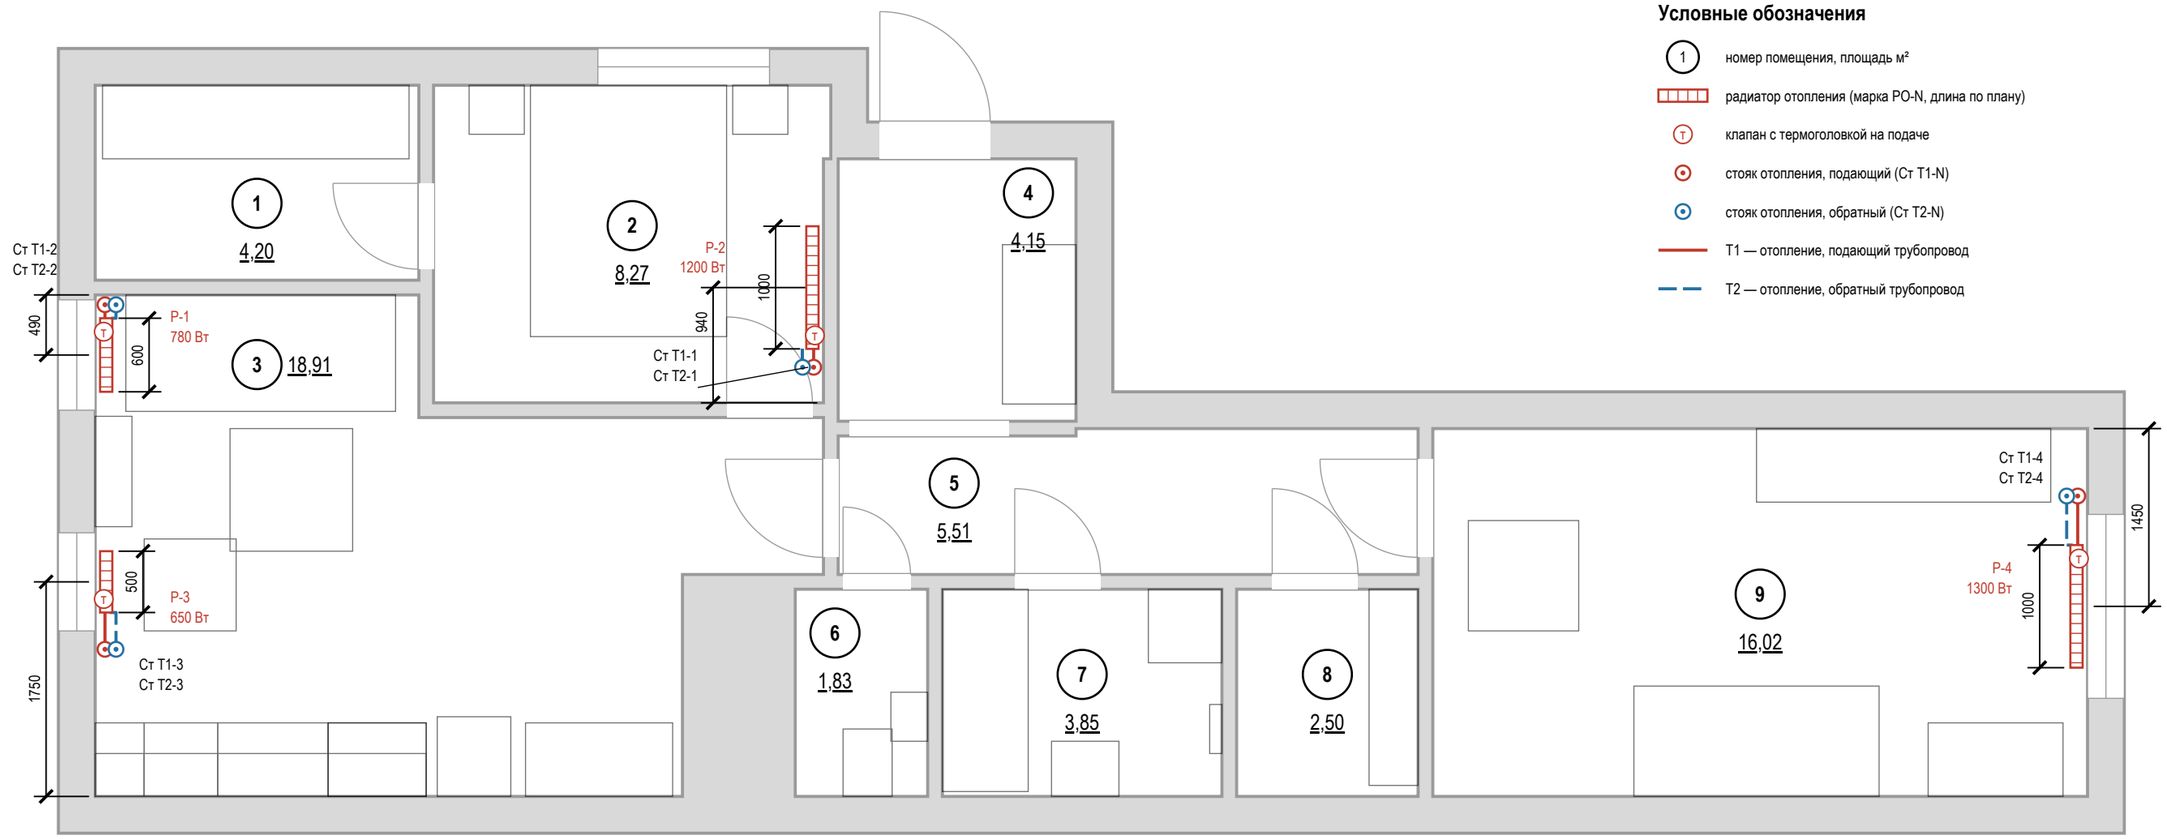

Условные обозначения

- (1) — номер помещения, площадь м²
- радиатор отопления (марка РО-N, длина по плану)
- (T) — клапан с термоголовкой на подаче
- стояк отопления, подающий (Ст Т1-N)
- стояк отопления, обратный (Ст Т2-N)
- Т1 — отопление, подающий трубопровод
- Т2 — отопление, обратный трубопровод

Примечания

1. Расчёт системы отопления, теплопотерь и подбор приборов — проектная организация с допуском СРО; лист даёт места и привязки.
2. Тип, длина и мощность радиаторов — по теплотехническому расчёту; лист задаёт места, зазоры и подключение.
3. Зазоры радиатора: низ не менее 100 мм от чистого пола, верх не менее 100 мм до подоконника, 30–50 мм от стены до задней панели; центр по оси окна с допуском ±20 мм. Верх до подоконника — 180 мм.
4. Радиаторы не закрывать глухими коробами и мебелью; перенос и замена приборов в многоквартирном доме — переустройство, согласование с управляющей организацией (ЖК РФ ст. 25–26); вынос на лоджию запрещён.
5. Трубы отопления через межквартирные стены не прокладывать (СП 51.13330.2011, п. 9.19); через перекрытия и перегородки — в гильзах.
6. Привязки приборов и подводок — по паспортам приобретённых радиаторов и клапанов, до черновых работ.
7. Привязки — до обмера: Стояки отопления в исходных данных не заданы: показаны у откосов окон и у торцов приборов, подводки — принципиально. До черновых работ — обмер стояков и паспорта приборов; лист перевыпустить по факту.
8. До закрытия отделкой трубопроводы отопления испытать гидростатическим давлением с оформлением акта (СП 73.13330.2016, 7.2–7.3).

Допущения и предложения на листе

Основа листа: размеры сняты с растрового плана заказчика без размеров: масштаб восстановлен по площадям помещений (≈ 11,8 мм на пиксель), контрольный обмер не выполнен (К-1); высота потолка 2700 мм принята: на плане заказчика её нет (К-2); толщины стен 300 / 120 мм приняты по плану заказчика, не замерены (К-1); разрешённая мощность 15 кВт принята по типовым ТУ для квартиры, ТУ заказчиком не переданы (К-4); подрайон климата не задан — принят не северный (жилые от 2,5 м) (К-9).

Открытые вопросы и конфликты по листу: К-6.

См. лист открытых вопросов (лист 6, записи К-1, К-2, К-4, К-6; лист 7, запись К-9).

1000 мм · печать 1:1

Изм.	Кол.уч	Лист	№ док.	Подп.	Дата
Разраб.		Кырлан А.С.			14.11.26
Пров.					
ГИП					
Н. контр.					
Утв.					

ГД-2026-007-АИ

Квартира 65 м²

Общая площадь 65,24* м² · * размеры со скана, не замерены (реестр — л. 6–8, К-1)

Дизайн-проект интерьера

Стадия	Лист	Листов
РП	38	117

План отопления

М 1:50

Кырлан Александр Сергеевич

выпуск 14.11.2026 № 9cc0b98f36 · стр. 42 из 139

05

Водоснабжение и канализация

Кырлан Александр Сергеевич


выпуск 14.11.2026 № 9cc0b98f36 · стр. 43 из 139

План выводов сантехники


Выводы В1, Т3**, К1 · привязки от чистовых стен · высоты от чистого пола, мм

ПРЕДВАРИТЕЛЬНО · не для производства работ · открыто пунктов: 14 (реестр — л. 6–8)


Фрагмент 1. Кухня-гостиная, пом. 3 (М 1:40)

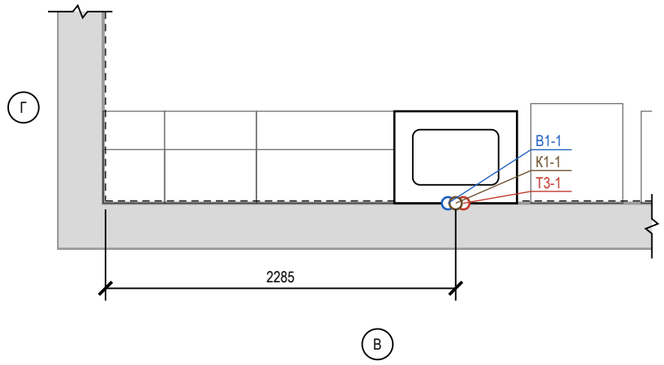

Фрагмент 2. Санузел, пом. 6 (М 1:40)

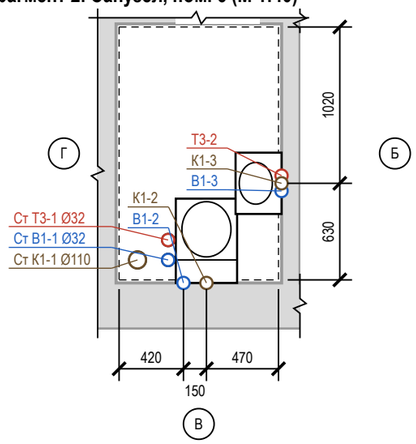

Фрагмент 3. Ванная, пом. 7 (М 1:40)

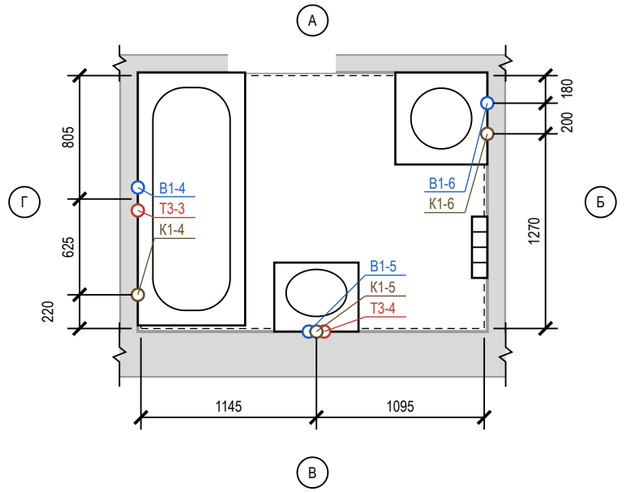

Ведомость привязок выводов

Код	Прибор	Ø	Н, мм	Привязка от чист. стен, мм	Прим.
В1-1	П4 мойка кухонная	½"	550	ст. В: 2235 от Г	межос. 100
Т3-1	—"	½"	550	ст. В: 2335 от Г	межос. 100
К1-1	—"	Ø50	400	ст. В: 2285 от Г	
В1-2	П20 унитаз подвесной	½"	1000	ст. В: 420 от Г	в раме инсталляции
К1-2	—"	Ø110	220	ст. В: 470 от Б	
В1-3	П21 умывальник	½"	550	ст. Б: 580 от В	межос. 100
Т3-2	—"	½"	550	ст. Б: 680 от В	межос. 100
К1-3	—"	Ø50	500	ст. Б: 630 от В	
В1-4	П1 ванна	½"	800	ст. Г: 730 от А	межос. 150
Т3-3	—"	½"	800	ст. Г: 770 от В	межос. 150
К1-4	—"	Ø50	50	ст. Г: 220 от В	
В1-5	П3 умывальник	½"	550	ст. В: 1095 от Г	межос. 100
Т3-4	—"	½"	550	ст. В: 1045 от Б	межос. 100
К1-5	—"	Ø50	500	ст. В: 1095 от Б	
В1-6	П22 стиральная машина	½"	800	ст. Б: 180 от А	кран машины
К1-6	—"	Ø50	600	ст. Б: 380 от А	

* — высота по практике монтажа; сверить по паспорту прибора

Условные обозначения

- вывод В1 (код — в ведомости привязок)
- вывод Т3 (код — в ведомости привязок)
- вывод К1 (код — в ведомости привязок)
- сантехприбор по расстановке (габарит модели)
- чистовая поверхность стены (от неё привязки)
- стояк «Ст К1-N / Ст В1-N» (ГОСТ 21.601), Ø мм
- линия обрыва (граница фрагмента)
- А — обозначение стены А–Г (как на развёртках)

Допущения и предложения на листе. Основа листа: размеры сняты с растрового плана заказчика без размеров: масштаб восстановлен по площадям помещений (≈ 11,8 мм на пиксель), контрольный обмер не выполнен (К-1); высота потолка 2700 мм принята: на плане заказчика её нет (К-2); толщины стен 300 / 120 мм приняты по плану заказчика, не замерены (К-1); разрешённая мощность 15 кВт принята по типовым ТУ для квартиры, ТУ заказчиком не переданы (К-4); подрайон климата не задан — принят не северный (жилые от 2,5 м) (К-9). Знак «**» — предложение проектировщика, заказчиком не утверждено (согласовать с заказчиком). См. лист открытых вопросов (лист 6, записи К-1, К-2, К-4; лист 7, запись К-9; лист 8, запись ИЗ-4).

Примечания

1. Привязки выводов даны от чистовых поверхностей стен (облицовка на сторону: кухня-гостиная — 15 мм (по данным); санузел — 20 мм (по данным); ванная — 20 мм (по данным)); эти же грани — на развёртках и в раскладке плитки. Высоты — от чистого пола помещения.
2. Высоты и межосевые, отмеченные «*», приняты по практике монтажа; до черновой разводки сверить по паспорту выбранного прибора (смеситель, инсталляция, сифон).
3. Горячая вода (Т3**) — слева от холодной (В1), если смотреть на прибор. Допуск установки выводов: ±5 мм в группе, ±20 мм у отдельно стоящих.
4. Расчёт систем водоснабжения и канализации и подбор оборудования выполняет проектная организация; лист задаёт места и высоты выводов.
5. Стояки в коробах/шахтах не замоноличивать; стояк К1 в коробе — звукоизоляция стояка в коробе без жёсткого контакта с трубой; к арматуре и ревизиям — люк не меньше 300×400.

1000 мм · печать 1:1

Изм.	Кол.уч	Лист	№ док.	Подп.	Дата
Разраб.		Кырлан А.С.			14.11.26
Пров.					
ГИП					
Н. контр.					
Утв.					

ГД-2026-007-АИ

Квартира 65 м²

Общая площадь 65,24* м² · * размеры со скана, не замерены (реестр — л. 6–8, К-1)

Дизайн-проект интерьера

Стадия	Лист	Листов
РП	39	117

План выводов сантехники

М 1:40

Кырлан Александр Сергеевич


выпуск 14.11.2026 № 9cc0b98f36 · стр. 44 из 139

Схема разводки водопровода и канализации


Схемы систем В1, Т3**, К1 · трассы принципиальные · уклоны в мм на 1 м · план М 1:400, фрагменты М 1:25

ПРЕДВАРИТЕЛЬНО · не для производства работ · открыто пунктов: 14 (реестр — л. 6–8)


План квартиры (М 1:400)

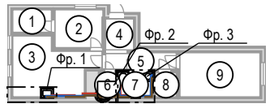


Фр. 1. Кухня-гостиная (М 1:25)

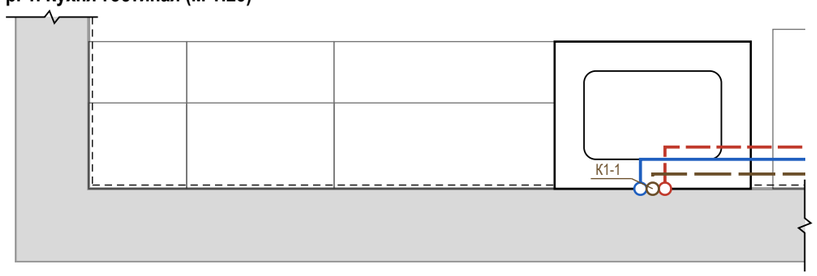

Фр. 2. Санузел (М 1:25)

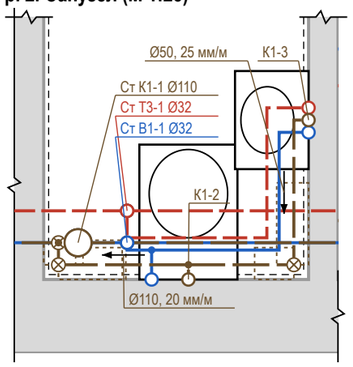

Фр. 3. Ванная (М 1:25)

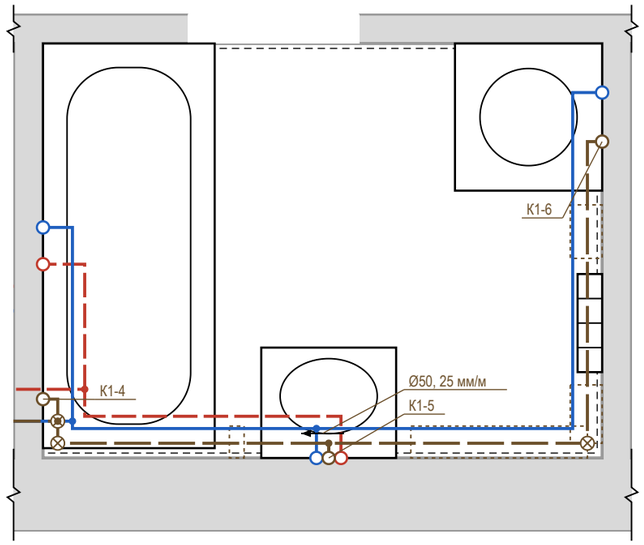

Допущения и предложения на листе

Основа листа: размеры сняты с растрового плана заказчика без размеров: масштаб восстановлен по площадям помещений (≈ 11,8 мм на пиксель), контрольный обмер не выполнен (К-1); высота потолка 2700 мм принята: на плане заказчика её нет (К-2); толщины стен 300 / 120 мм приняты по плану заказчика, не замерены (К-1); разрешённая мощность 15 кВт принята по типовым ТУ для квартиры, ТУ заказчиком не переданы (К-4); подрайон климата не задан — принят не северный (жилые от 2,5 м) (К-9).

Знак «**» — предложение проектировщика, заказчиком не утверждено (согласовать с заказчиком): ИЗ-4: Т3.

Открытые вопросы и конфликты по листу: К-12.

См. лист открытых вопросов (лист 6, записи К-1, К-2, К-4; лист 7, записи К-9, К-12; лист 8, запись ИЗ-4).

Условные обозначения


- В1 — водопровод хозяйственно-питьевой (ХВС), PP-R Ø20
- Т3 — горячее водоснабжение, подача (ГВС), PP-R Ø20
- К1 — канализация бытовая
- направление уклона К1 / пола: Ø, мм на 1 м
- ⊗ ревизия (прочистка) К1 — доступ сохранить
- ● тройник (ответвление к прибору)
- короб К1 над чистым полом (ГКЛВ под плитку)
- ○ вывод В1 (код — в ведомости привязок)
- ○ вывод Т3 (код — в ведомости привязок)
- ○ вывод К1 (код — в ведомости привязок)
- сантехприбор по расстановке (габарит модели)
- ◯ стояк «Ст К1-N / Ст В1-N» (ГОСТ 21.601), Ø мм
- линия обрыва (граница фрагмента)
- граница фрагмента на плане (Фр. N)

Профиль выпусков К1 (до врезки в стояк)

Выпуск	Прибор	Ø	L, м	i, мм/м	Δh, мм	Прокладка, мм
К1-2	П20 унитаз подвесной	Ø110	0,76	20	15	короб 160×140
К1-6	П22 стиральная машина	Ø50	4,66	25	117	короб 200×110
К1-1	П4 мойка кухонная	Ø50	3,70	25	93	над полом за приборами
К1-5	П3 умывальник	Ø50	2,38	25	59	над полом за приборами
К1-3	П21 умывальник	Ø50	1,78	25	45	короб 130×110
К1-4	П1 ванна	Ø50	1,27	25	32	над полом за приборами

Короб h×b: h — от чистого пола, b — от чистовой стены. Стяжка 90 мм — лист полов.

Узел ввода В1, Т3** (по данным, без масштаба)

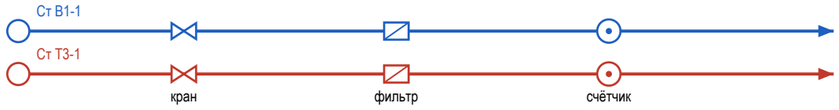

⊗ Ст К1-1: ревизия на стояке — люк в коробе

Примечания

1. Трассы принципиальные, построены от стояков вдоль стен помещений; фактическое положение фиксируется исполнительной схемой с привязками (фото с рулеткой) до закрытия.
2. Уклон К1 не менее 1/d и не более 150 мм/м (СП 30.13330.2020, п. 19.1), приняты практические уклоны; поворот — двумя отводами 45°, ревизия после поворота, доступ сохранить. Стояк К1 в коробе — звукоизоляция стояка в коробе, без жёсткого контакта короба с трубой.
3. Решение по К1: стяжка 90 мм не укрывает трубы (нужно Ø + Δh + 45 мм) — выпуски идут над чистым полом вдоль стен: К1-1, К1-5, К1-4 — за приборами и в раме инсталляции; К1-2, К1-6, К1-3 — в коробе ГКЛВ под плитку (размеры в профиле). Короба — на развёртках; отметку низа врезки в стояк замерить до черновых работ.
4. Отводы К1-6 (4,7 м) длиннее 4 м без вентиляции — у прибора воздушный клапан Ø50 в доступном месте (за люком или в тумбе) либо вентилируемый отвод (EN 12056-2, табл. 4); предложение проектировщика, подбор — проектная организация.
5. Узел ввода В1, Т3** — по данным проекта: кран → фильтр → счётчик. Доступ к арматуре — через люк не меньше 300×400. Водопровод — в штробе стен или в коробах; трубы испытать давлением до закрытия (акт скрытых работ).
6. Расчёт систем, диаметры магистралей и подбор оборудования выполняет проектная организация; врезка и перенос стояков — по согласованию с управляющей организацией. Арматуру и привязки сверить по паспортам приборов.
7. Ведомость выводов (код, прибор, высота, привязка) — лист 39; на схеме — только коды.

Изм.	Кол.уч	Лист	№ док.	Подп.	Дата
Разраб.		Кырлан А.С.			14.11.26
Пров.					
ГИП					
Н. контр.					
Утв.					

ГД-2026-007-АИ

Квартира 65 м²

Общая площадь 65,24* м² · * размеры со скана, не замерены (реестр — л. 6–8, К-1)

Дизайн-проект интерьера

Стадия	Лист	Листов
РП	40	117

Схема разводки водопровода и канализации

М 1:400; 1:25

Кырлан Александр Сергеевич


выпуск 14.11.2026 № 9cc0b98f36 · стр. 45 из 139

Аксонометрическая схема В1 (холодное водоснабжение)

аксонометрия · диаметры, уклоны, отметки, стояки и приборы · трассы принципиальные

Схема В1 (М 1:50)

ПРЕДВАРИТЕЛЬНО · не для производства работ · открыто пунктов: 14 (реестр — л. 6–8)

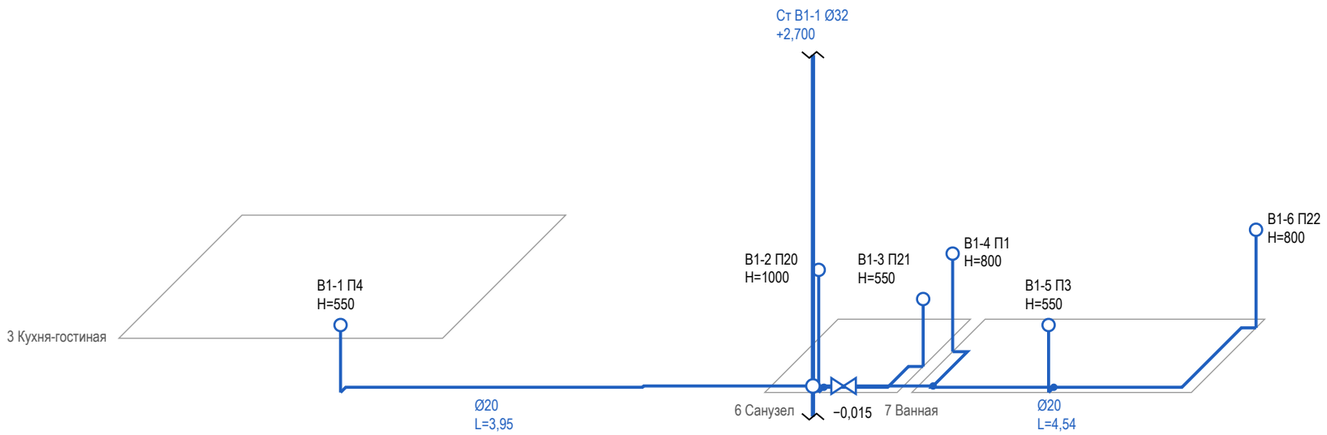

Ведомость выводов В1

Код	Прибор	Н, мм	Ø, мм	Трасса, м
В1-6	П22 стиральная машина	800	20	4,54
В1-1	П4 мойка кухонная	550	20	3,95
В1-5	П3 умывальник	550	20	0,12
В1-4	П1 ванна	800	20	0,91
В1-3	П21 умывальник	550	20	1,25
В1-2	П20 унитаз подвесной	1000	20	0,12

Условные обозначения

- В1 — водопровод хозяйственно-питьевой (ХВС), PP-R Ø20
- вывод В1 (код — в ведомости привязок)
- стояк «Ст К1-N / Ст В1-N» (ГОСТ 21.601), Ø мм
- стояк в плане (на отметке пола); вертикаль — стояк по высоте, разрыв — перекрытие
- тройник (ответвление к прибору)
- кран шаровой

Примечания

1. Схема В1 построена по тем же трассам, что план разводки: положение в плане сохранено, глубина — в масштабе ×0,5. Трассы принципиальные; фактическое положение фиксируется исполнительной схемой до закрытия.
2. Высоты Н — от чистого пола помещения, мм. Прокладка магистрали В1 по данным: в стяжке пола, в стяжке пола, выше плиты перекрытия; отметка трасс — по пирогу пола.
3. Узел ввода В1 (кран, фильтр, счётчик, обратный клапан, кран) — на схеме разводки; состав узла ввода — по согласованию. Кран шаровой — на первом участке от стояка.
4. Трубы испытать давлением до закрытия (акт скрытых работ, опрессовка по СП 73.13330.2016).
5. Диаметры, высоты выводов и места кранов — по паспортам выбранных приборов и расчёту проектной организации.
6. Расчёт систем, диаметры магистралей и подбор оборудования выполняет проектная организация.

Допущения и предложения на листе. См. лист открытых вопросов (листы 6–8).

1000 мм · печать 1:1

Изм.	Кол.уч	Лист	№ док.	Подп.	Дата
Разраб.		Кырлан А.С.			14.11.26
Пров.					
ГИП					
Н. контр.					
Утв.					

ГД-2026-007-АИ

Квартира 65 м²

Общая площадь 65,24* м² · * размеры со скана, не замерены (реестр — л. 6–8, К-1)

Дизайн-проект интерьера

Стадия	Лист	Листов
РП	41	117

Аксонометрическая схема В1 (холодное водоснабжение)

М 1:50

Кырлан Александр Сергеевич


выпуск 14.11.2026 № 9cc0b98f36 · стр. 46 из 139

Аксонометрическая схема Т3 (горячее водоснабжение)

аксонометрия · диаметры, уклоны, отметки, стояки и приборы · трассы принципиальные

Схема Т3 (М 1:50)**

ПРЕДВАРИТЕЛЬНО · не для производства работ · открыто пунктов: 14 (реестр — л. 6–8)

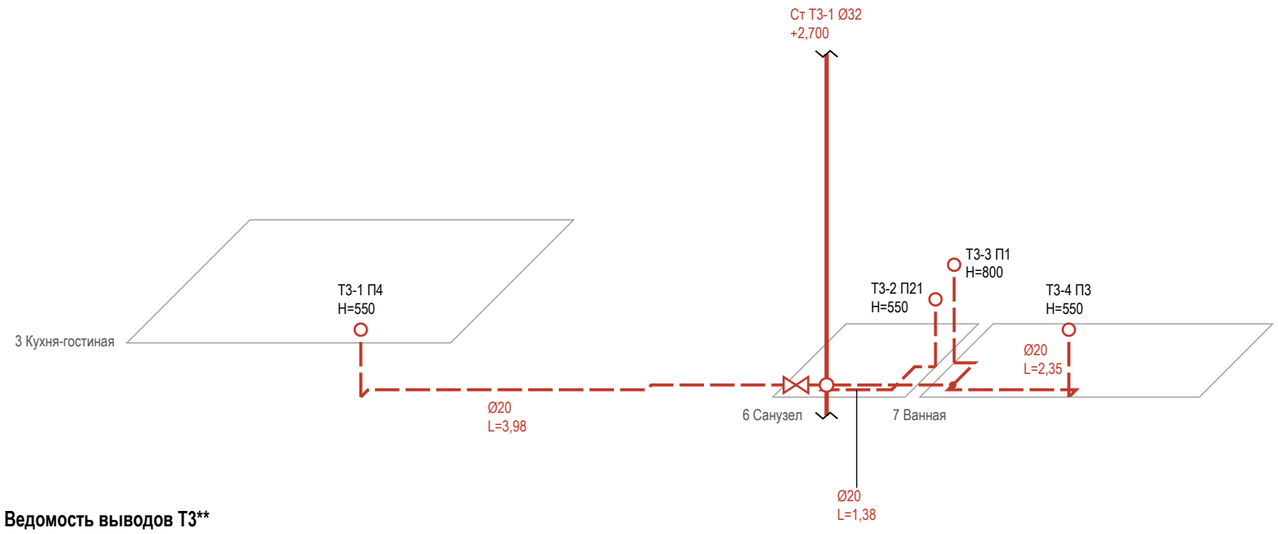

Ведомость выводов Т3**

Код	Прибор	H, мм	Ø, мм	Трасса, м
Т3-1	П4 мойка кухонная	550	20	3,98
Т3-4	П3 умывальник	550	20	2,35
Т3-3	П1 ванна	800	20	0,68
Т3-2	П21 умывальник	550	20	1,38

Условные обозначения

- Т3 — горячее водоснабжение, подача (ГВС), PP-R Ø20
- вывод Т3 (код — в ведомости привязок)
- стояк «Ст К1-N / Ст В1-N» (ГОСТ 21.601), Ø мм
- стояк в плане (на отметке пола); вертикаль — стояк по высоте, разрыв — перекрытие
- тройник (ответвление к прибору)
- кран шаровой

Примечания

1. Схема Т3** построена по тем же трассам, что план разводки: положение в плане сохранено, глубина — в масштабе ×0,5. Трассы принципиальные; фактическое положение фиксируется исполнительной схемой до закрытия.
2. Высоты H — от чистого пола помещения, мм. Прокладка магистрали Т3** по данным: в стяжке пола, в стяжке пола, выше плиты перекрытия; отметка трасс — по пирогу пола.
3. Узел ввода Т3** (кран, фильтр, счётчик, обратный клапан, кран) — на схеме разводки; состав узла ввода — по согласованию. Кран шаровой — на первом участке от стояка.
4. Циркуляция ГВС в данных не задана — циркуляционного трубопровода на схеме нет (запись реестра К-12).
5. Трубы испытать давлением до закрытия (акт скрытых работ, опрессовка по СП 73.13330.2016).
6. Диаметры, высоты выводов и места кранов — по паспортам выбранных приборов и расчёту проектной организации.
7. Расчёт систем, диаметры магистралей и подбор оборудования выполняет проектная организация.

1000 мм · печать 1:1

Допущения и предложения на листе. Знак «**» предложено (согласовать). См. лист открытых вопросов (листы 6–8).

Изм.	Кол.уч	Лист	№ док.	Подп.	Дата
Разраб.		Кырлан А.С.			14.11.26
Пров.					
ГИП					
Н. контр.					
Утв.					

ГД-2026-007-АИ

Квартира 65 м²

Общая площадь 65,24* м² · * размеры со скана, не замерены (реестр — л. 6–8, К-1)

Дизайн-проект интерьера	Стадия	Лист	Листов
	РП	42	117

Аксонометрическая схема Т3 (горячее водоснабжение)
М 1:50

Кырлан Александр Сергеевич


выпуск 14.11.2026 № 9cc0b98f36 · стр. 47 из 139

Аксонометрическая схема К1 (канализация)

аксонометрия · диаметры, уклоны, отметки, стояки и приборы · трассы принципиальные

Схема К1 (М 1:50)

ПРЕДВАРИТЕЛЬНО · не для производства работ · открыто пунктов: 14 (реестр — л. 6–8)

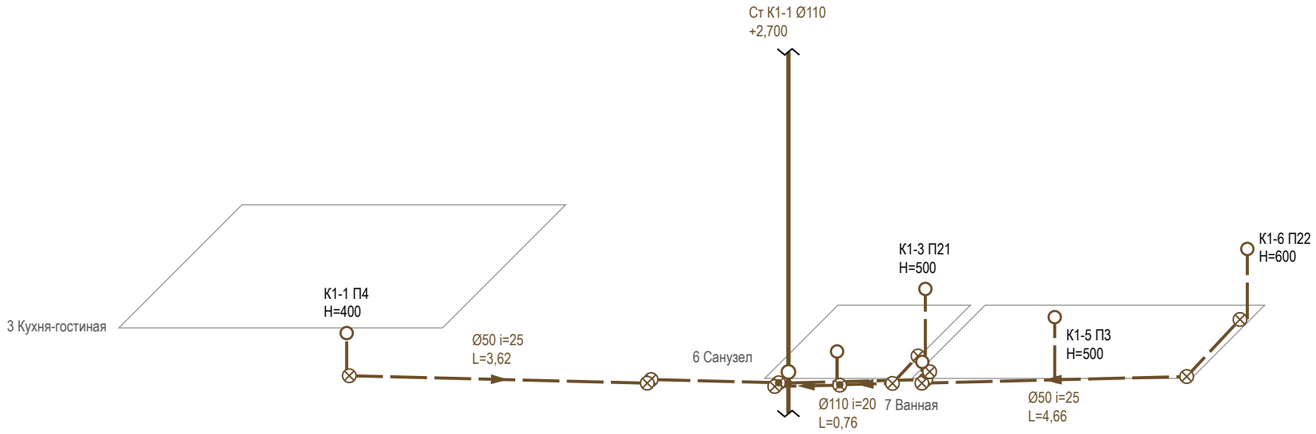

Ведомость выводов К1

Код	Прибор	H, мм	Ø, i	Трасса, м
К1-2	П20 унитаз подвесной	220	110 i=20	0,76
К1-6	П22 стиральная машина	600	50 i=25	4,66
К1-1	П4 мойка кухонная	400	50 i=25	3,62
К1-5	П3 умывальник	500	50 i=25	0,06
К1-3	П21 умывальник	500	50 i=25	1,08
К1-4	П1 ванна	50	50 i=25	0,15

Условные обозначения

- К1 — канализация бытовая
- вывод К1 (код — в ведомости привязок)
- стояк «Ст К1-N / Ст В1-N» (ГОСТ 21.601), Ø мм
- стояк в плане (на отметке пола); вертикаль — стояк по высоте, разрыв — перекрытие
- направление уклона К1 / пола: Ø, мм на 1 м
- ⊗ ревизия (прочистка) К1 — доступ сохранить
- • тройник (ответвление к прибору)

Примечания

1. Схема К1 построена по тем же трассам, что план разводки: положение в плане сохранено, глубина — в масштабе ×0,5. Трассы принципиальные; фактическое положение фиксируется исполнительной схемой до закрытия.
2. Отметки — от плиты перекрытия: низ трубы у врезки в стояк — отметка из данных выпуска, к прибору труба поднимается на уклон i, мм/м (уклон не менее 1/d и не более 150 мм/м, СП 30.13330.2020, п. 19.1); чистый пол — выше плиты на стяжку (высота пирога пола). Высота выпуска прибора H — от чистого пола.
3. Ревизия — на повороте и в начале участка; стояк К1 в коробе с люком — звукоизоляция стояка в коробе; поворот — двумя отводами 45°.
4. Трубы испытать давлением до закрытия (акт скрытых работ, опрессовка по СП 73.13330.2016).
5. Диаметры, высоты выводов и места кранов — по паспортам выбранных приборов и расчёту проектной организации.
6. Расчёт систем, диаметры магистралей и подбор оборудования выполняет проектная организация.

Допущения и предложения на листе. См. лист открытых вопросов (листы 6–8).

1000 мм · печать 1:1

Изм.	Кол.уч	Лист	№ док.	Подп.	Дата
Разраб.		Кырлан А.С.			14.11.26
Пров.					
ГИП					
Н. контр.					
Утв.					

ГД-2026-007-АИ

Квартира 65 м²

Общая площадь 65,24* м² · * размеры со скана, не замерены (реестр — л. 6–8, К-1)

Дизайн-проект интерьера

Стадия	Лист	Листов
РП	43	117

Аксонометрическая схема К1 (канализация)

М 1:50

Кырлан Александр Сергеевич


выпуск 14.11.2026 № 9cc0b98f36 · стр. 48 из 139

Развёртки мокрых зон: выводы ВК. Кухня-гостиная

пом. 3 · выводы В1, Т3**, К1 на стенах · высоты от чистого пола, привязки от чистовых углов, мм

ПРЕДВАРИТЕЛЬНО · не для производства работ · открыто пунктов: 14 (реестр — л. 6–8)

Стена В (М 1:20)

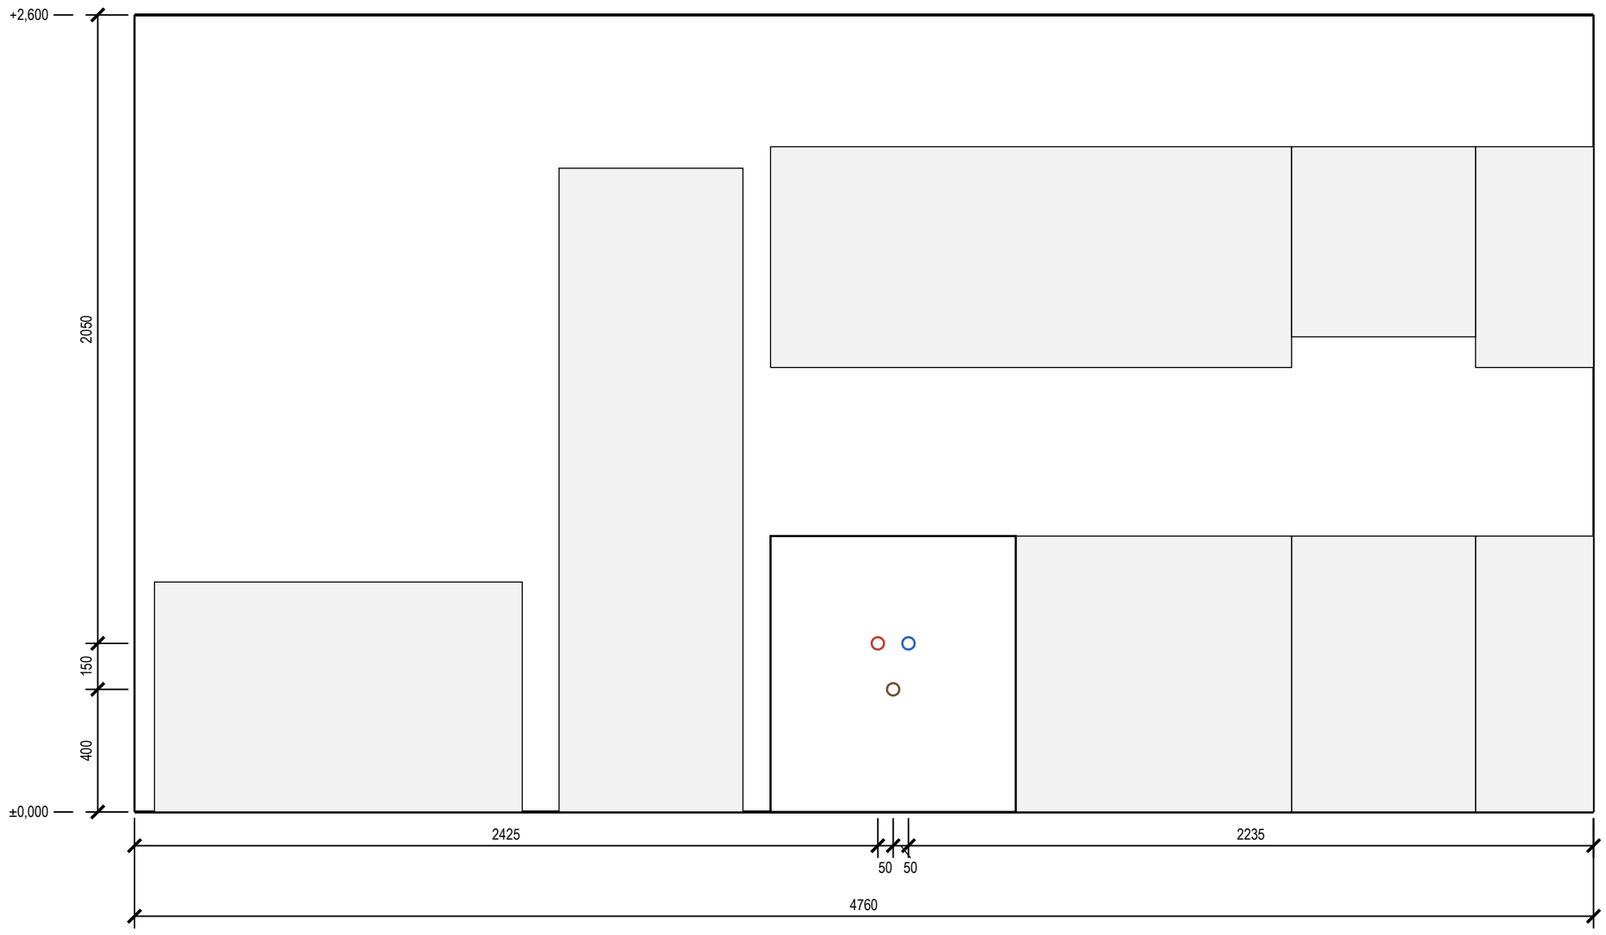

Допущения и предложения на листе

Основа листа: размеры сняты с растрового плана заказчика без размеров: масштаб восстановлен по площадям помещений (≈ 11,8 мм на пиксель), контрольный обмер не выполнен (К-1); высота потолка 2700 мм принята: на плане заказчика её нет (К-2); толщины стен 300 / 120 мм приняты по плану заказчика, не замерены (К-1); разрешённая мощность 15 кВт принята по типовым ТУ для квартиры, ТУ заказчиком не переданы (К-4); подрайон климата не задан — принят не северный (жилые от 2,5 м) (К-9).
Знак «**» — предложение проектировщика, заказчиком не утверждено (согласовать с заказчиком): И3-4: Т3.
Открытые вопросы и конфликты по листу: К-12.
См. лист открытых вопросов (лист 6, записи К-1, К-2, К-4; лист 7, записи К-9, К-12; лист 8, запись И3-4).

Ведомость привязок выводов (от чистого пола и угла)

Код	Прибор	Ø	H, мм	Привязка, мм
В1-1	П4 мойка кухонная	½"	550	ст. В: 2525 от лев. угла
Т3-1	П4 мойка кухонная	½"	550	ст. В: 2425 от лев. угла
К1-1	П4 мойка кухонная	Ø50	400	ст. В: 2475 от лев. угла

Условные обозначения

- вывод В1 (код — в ведомости привязок)
- вывод Т3 (код — в ведомости привязок)
- вывод К1 (код — в ведомости привязок)
- сантехприбор по расстановке (габарит модели)
- дверной проём; окно — сплошной контур

Примечания

1. Габариты и высоты приборов, межосевые смесителей и места кранов — по паспортам выбранных приборов, сверяются до разметки стен.
2. Высоты H — от чистого пола помещения, мм; отметка чистого пола и потолка — у левого края вида (от ±0,000 объекта). Привязки — от левого чистового угла вида (облицовка стен вычтена), как на развёртках стен.
3. Ревизионные люки (арматура и ревизии у П4 300×400, стена В у П4, предложение): привязка к углу — по раскладке плитки, подтверждается обмером.
4. Ревизионные люки к арматуре и ревизиям в данных не заданы: место и размер не определены (записи реестра нет).
5. Мойка, ПММ и фильтр — выводы в шкафу мойки; диаметры и положение сифона и кранов сверить по паспортам приборов и чертежам модуля.
6. Часть подписей выводов не уместилась у знака: коды и высоты — в ведомости привязок.
7. Расчёт систем водоснабжения и канализации и подбор оборудования выполняет проектная организация; лист задаёт места и высоты выводов.

1000 мм · печать 1:1

Изм.	Кол.уч	Лист	№ док.	Подп.	Дата
Разраб.		Кырлан А.С.			14.11.26
Пров.					
ГИП					
Н. контр.					
Утв.					

ГД-2026-007-АИ

Квартира 65 м²

Общая площадь 65,24* м² · * размеры со скана, не замерены (реестр — л. 6–8, К-1)

Дизайн-проект интерьера

Стадия	Лист	Листов
РП	44	117

Развёртки мокрых зон: выводы ВК. Кухня-гостиная

М 1:20

Кырлан Александр Сергеевич


выпуск 14.11.2026 № 9cc0b98f36 · стр. 49 из 139

Развёртки мокрых зон: выводы ВК. Санузел


пом. 6 · выводы В1, Т3**, К1 на стенах · высоты от чистого пола, привязки от чистовых углов, мм

ПРЕДВАРИТЕЛЬНО · не для производства работ · открыто пунктов: 14 (реестр — л. 6–8)

Стена Б (М 1:20)

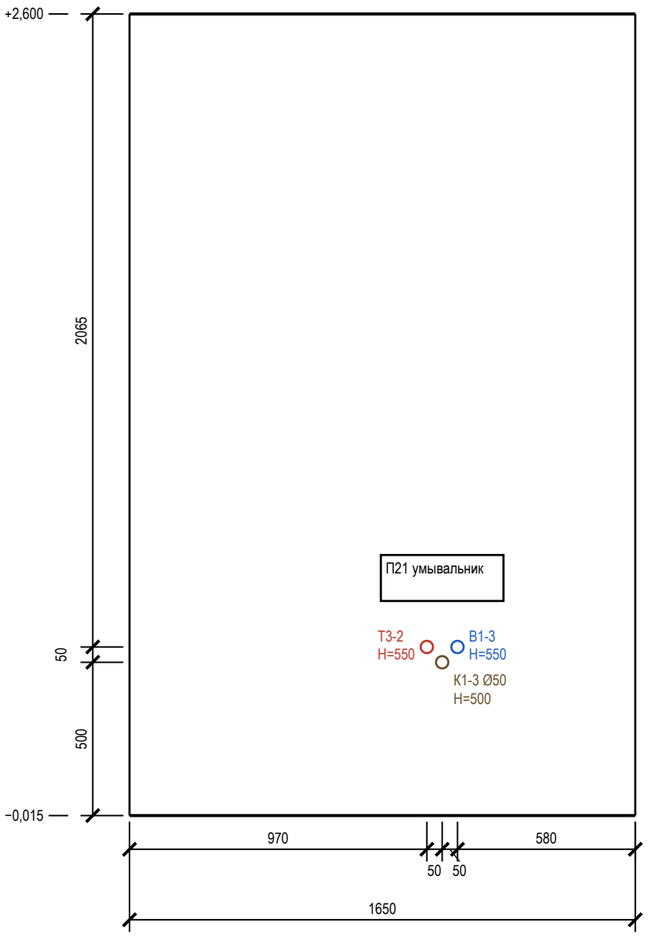

Стена В (М 1:20)

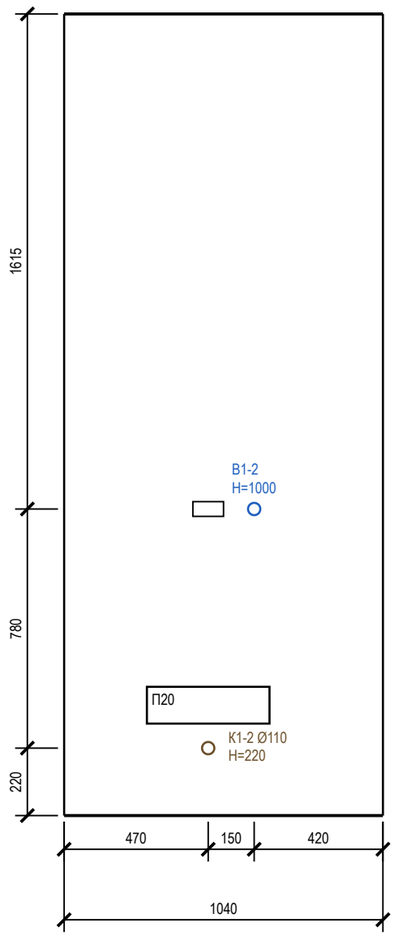

Допущения и предложения на листе

Основа листа: размеры сняты с растрового плана заказчика без размеров: масштаб восстановлен по площадям помещений (≈ 11,8 мм на пиксель), контрольный обмер не выполнен (К-1); высота потолка 2700 мм принята: на плане заказчика её нет (К-2); толщины стен 300 / 120 мм приняты по плану заказчика, не замерены (К-1); разрешённая мощность 15 кВт принята по типовым ТУ для квартиры, ТУ заказчиком не переданы (К-4); подрайон климата не задан — принят не северный (жилые от 2,5 м) (К-9).
Знак «**» — предложение проектировщика, заказчиком не утверждено (согласовать с заказчиком): ИЗ-4: Т3.
Открытые вопросы и конфликты по листу: К-12.
См. лист открытых вопросов (лист 6, записи К-1, К-2, К-4; лист 7, записи К-9, К-12; лист 8, запись ИЗ-4).

Ведомость привязок выводов (от чистого пола и угла)

Код	Прибор	Ø	H, мм	Привязка, мм
В1-3	П21 умывальник	½"	550	ст. Б: 1070 от лев. угла
Т3-2	П21 умывальник	½"	550	ст. Б: 970 от лев. угла
К1-3	П21 умывальник	Ø50	500	ст. Б: 1020 от лев. угла

Ведомость привязок (продолжение)

Код	Прибор	Ø	H, мм	Привязка, мм
В1-2	П20 унитаз подвесной	½"	1000	ст. В: 620 от лев. угла
К1-2	П20 унитаз подвесной	Ø110	220	ст. В: 470 от лев. угла

Условные обозначения

- вывод В1 (код — в ведомости привязок)
- вывод Т3 (код — в ведомости привязок)
- вывод К1 (код — в ведомости привязок)
- сантехприбор по расстановке (габарит модели)
- дверной проём; окно — сплошной контур
- кнопка смыва инсталляции (H — по данным прибора)

Примечания

1. Габариты и высоты приборов, межосевые смесителей и места кранов — по паспортам выбранных приборов, сверяются до разметки стен.
2. Высоты H — от чистого пола помещения, мм; отметка чистого пола и потолка — у левого края вида (от ±0,000 объекта). Привязки — от левого чистового угла вида (облицовка стен вычтена), как на развёртках стен.
3. Кнопка смыва П20 — H=1000 (по данным прибора).
4. Стояки в помещении: Ст К1-1 Ø110, Ст В1-1 Ø32, Ст Т3-1 Ø32 — положение на плане выводов; выводы подключаются к ним по схеме разводки.
5. Ревизионные люки (арматура и ревизии у П20 300×400, стена В у П20, предложение): привязка к углу — по раскладке плитки, подтверждается обмером.
6. Ревизионные люки к арматуре и ревизиям в данных не заданы: место и размер не определены (записи реестра нет).
7. Расчёт систем водоснабжения и канализации и подбор оборудования выполняет проектная организация; лист задаёт места и высоты выводов.

1000 мм · печать 1:1

Изм.	Кол.уч	Лист	№ док.	Подп.	Дата
Разраб.		Кырлан А.С.			14.11.26
Пров.					
ГИП					
Н. контр.					
Утв.					

ГД-2026-007-АИ

Квартира 65 м²

Общая площадь 65,24* м² · * размеры со скана, не замерены (реестр — л. 6–8, К-1)

Дизайн-проект интерьера

Стадия	Лист	Листов
РП	45	117

Развёртки мокрых зон: выводы ВК. Санузел

М 1:20

Кырлан Александр Сергеевич


выпуск 14.11.2026 № 9cc0b98f36 · стр. 50 из 139

Развёртки мокрых зон: выводы ВК. Ванная


пом. 7 · выводы В1, Т3**, К1 на стенах · высоты от чистого пола, привязки от чистовых углов, мм

ПРЕДВАРИТЕЛЬНО · не для производства работ · открыто пунктов: 14 (реестр — л. 6–8)


Стена Б (М 1:25)

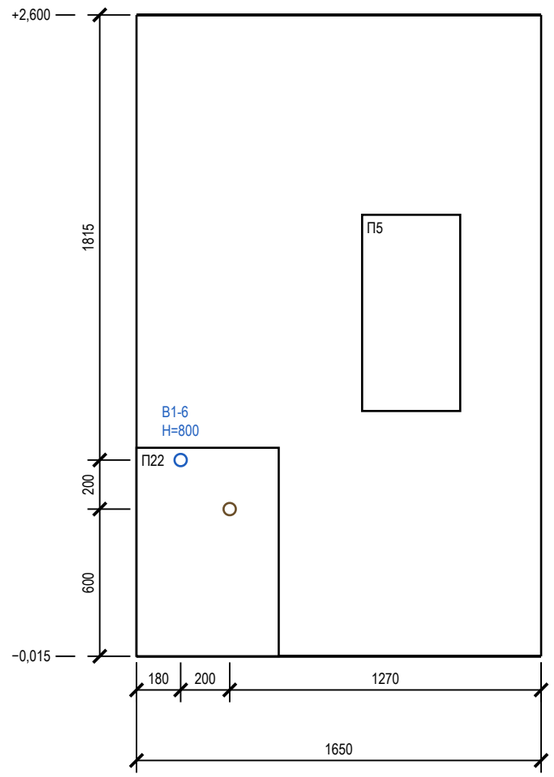

Стена В (М 1:25)

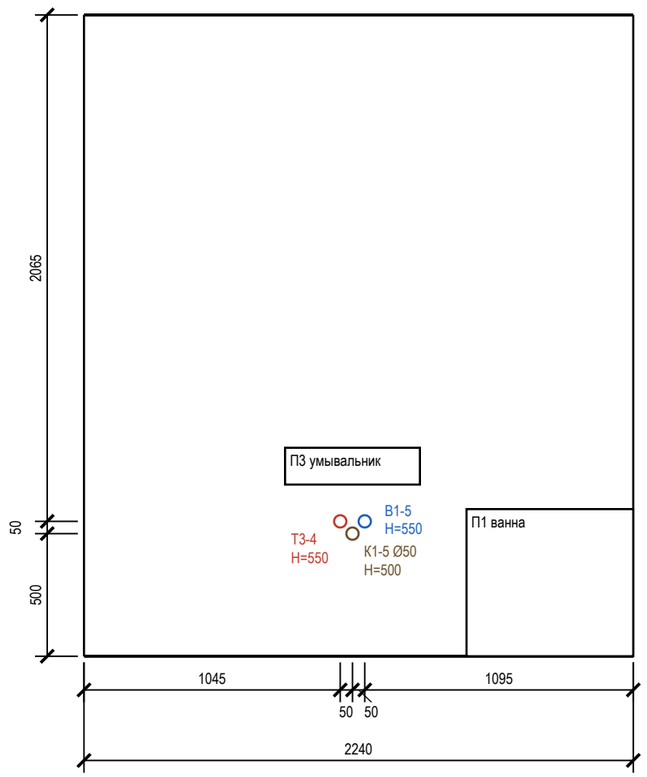

Стена Г (М 1:25)

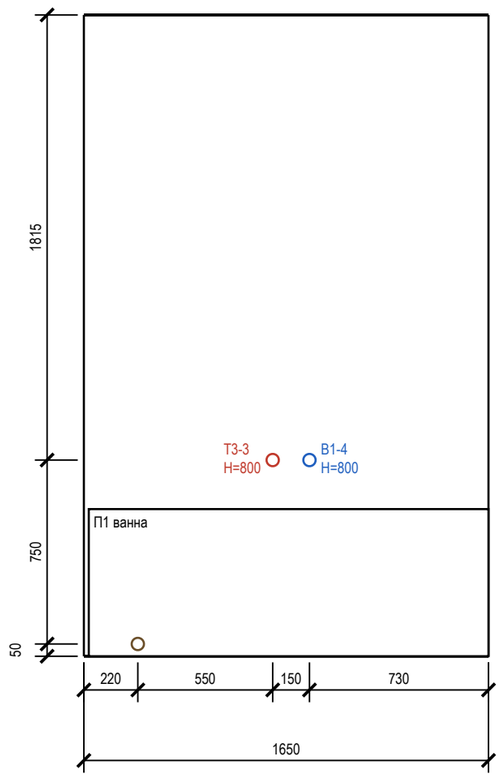

Допущения и предложения на листе

Основа листа: размеры сняты с растрового плана заказчика без размеров: масштаб восстановлен по площадям помещений (≈ 11,8 мм на пиксель), контрольный обмер не выполнен (К-1); высота потолка 2700 мм принята: на плане заказчика её нет (К-2); толщины стен 300 / 120 мм приняты по плану заказчика, не замерены (К-1); разрешённая мощность 15 кВт принята по типовым ТУ для квартиры, ТУ заказчиком не переданы (К-4); подрайон климата не задан — принят не северный (жилые от 2,5 м) (К-9).

Знак «**» — предложение проектировщика, заказчиком не утверждено (согласовать с заказчиком): ИЗ-4: Т3.

Открытые вопросы и конфликты по листу: К-12.

См. лист открытых вопросов (лист 6, записи К-1, К-2, К-4; лист 7, записи К-9, К-12; лист 8, запись ИЗ-4).

Ведомость привязок выводов (от чистого пола и угла)

Код	Прибор	Ø	H, мм	Привязка, мм
В1-6	П22 стиральная машина	½"	800	ст. Б: 180 от лев. угла
К1-6	П22 стиральная машина	Ø50	600	ст. Б: 380 от лев. угла
В1-5	П3 умывальник	½"	550	ст. В: 1145 от лев. угла
Т3-4	П3 умывальник	½"	550	ст. В: 1045 от лев. угла
К1-5	П3 умывальник	Ø50	500	ст. В: 1095 от лев. угла
В1-4	П1 ванна	½"	800	ст. Г: 920 от лев. угла
Т3-3	П1 ванна	½"	800	ст. Г: 770 от лев. угла
К1-4	П1 ванна	Ø50	50	ст. Г: 220 от лев. угла

Условные обозначения

- вывод В1 (код — в ведомости привязок)
- вывод Т3 (код — в ведомости привязок)
- вывод К1 (код — в ведомости привязок)
- сантехприбор по расстановке (габарит модели)
- дверной проём; окно — сплошной контур

Примечания

1. Габариты и высоты приборов, межосевые смесителей и места кранов — по паспортам выбранных приборов, сверяются до разметки стен.
2. Высоты H — от чистого пола помещения, мм; отметка чистого пола и потолка — у левого края вида (от ±0,000 объекта). Привязки — от левого чистового угла вида (облицовка стен вычтена), как на развёртках стен.
3. Ревизионные люки (арматура и ревизии у П1 300×400, стена Г у П1, предложение): привязка к углу — по раскладке плитки, подтверждается обмером.
4. Ревизионные люки к арматуре и ревизиям в данных не заданы: место и размер не определены (записи реестра нет).
5. Часть подписей выводов не уместилась у знака: коды и высоты — в ведомости привязок.
6. Стены А: выводов В1, Т3**, К1 нет — развёртка не строится (иначе лист-продолжение); приборы и проёмы этих стен — на плане выводов и развёртках стен чертёжника.
7. Расчёт систем водоснабжения и канализации и подбор оборудования выполняет проектная организация; лист задаёт места и высоты выводов.

1000 мм · печать 1:1

Изм.	Кол.уч	Лист	№ док.	Подп.	Дата
Разраб.		Кырлан А.С.			14.11.26
Пров.					
ГИП					
Н. контр.					
Утв.					

ГД-2026-007-АИ

Квартира 65 м²

Общая площадь 65,24* м² · * размеры со скана, не замерены (реестр — л. 6–8, К-1)

Дизайн-проект интерьера

Стадия	Лист	Листов
РП	46	117

Развёртки мокрых зон: выводы ВК. Ванная

М 1:25

Кырлан Александр Сергеевич

выпуск 14.11.2026 № 9cc0b98f36 · стр. 51 из 139

Спецификация сантехнического оборудования

Форма 1 ГОСТ 21.110-2013 · ГД-2026-007-АИ-ВК.СО · приборы, арматура, трубопроводы

ПРЕДВАРИТЕЛЬНО · не для производства работ · открыто пунктов: 14 (реестр — л. 6–8)

Поз.	Наименование и техническая характеристика	Тип, марка, обозначение документа	Код продукции	Поставщик	Ед. изм.	Кол.	Масса 1 ед., кг	Примечание
	Санитарные приборы							
1	Ванна встраиваемая акриловая 1650×700 мм, с каркасом, экраном и отверстием слив-перелив	Ravak Classic C541000000		выбор заказчика	шт	1		П1
2	Унитаз подвесной безободковый, с сиденьем микролифт, крепёж и звукоизолирующая прокладка	Jacob Delafon Struktura EDF102-00		выбор заказчика	шт	1		П20
3	Инсталляция для подвесного унитаза: рама высотой 1120 мм, бачок, клавиша смыва (ось клавиши 1050 мм от чистого пола)	аналог		выбор заказчика	шт	1		П20; короб ГКЛВ
4	Умывальник подвесной 400×300 мм, с отверстием под смеситель и переливом	Roca The Gap 7.3274.7.400.0		выбор заказчика	шт	1		П21
5	Умывальник подвесной 550×450 мм, с отверстием под смеситель и переливом	Roca The Gap 7.3274.7.400.0		выбор заказчика	шт	1		П3
6	Мойка кухонная 700×480 мм, с переливом	мойка врезная 700×480 в шкафу М6		с кухонной мебелью	шт	1		П4
7	Полотенцесушитель электрический, IP44, с терморегулятором	аналог		выбор заказчика	шт	1		П5
	Смесители, сифоны и арматура приборов							
8	Смеситель для ванны настенный однорычажный, межосевое 150 мм, с душевым набором (лейка, шланг, держатель)	аналог		выбор заказчика	шт	1		П1
9	Смеситель для умывальника однорычажный, с донным клапаном	аналог		выбор заказчика	шт	2		П21, П3
10	Смеситель кухонный однорычажный, высокий излив	аналог		выбор заказчика	шт	1		П4
11	Обвязка ванны слив-перелив Ø40/50 с сифоном	аналог		выбор заказчика	шт	1		П1
12	Сифон для умывальника бутылочный Ø32/40–50, с гофрой к выпуску	аналог		выбор заказчика	шт	2		П21, П3
13	Сифон для мойки Ø40/50	аналог		выбор заказчика	шт	1		П4
14	Сифон для стиральной машины встраиваемый в стену Ø50, с обратным клапаном	аналог		выбор заказчика	шт	1		П22
15	Кран угловой ½"×½" с гибкой подводкой 40 см (умывальники, мойка)	аналог		выбор заказчика	шт	6		по 2 на прибор
16	Кран шаровой угловой ½"×¾" для подключения стиральной и посудомоечной машины	аналог		выбор заказчика	шт	1		П22
	Трубопроводы							
17	Труба полипропиленовая PP-R PN20 Ø20×3,4 (В1)	ГОСТ 32415-2013		выбор заказчика	м	17	0,17	10,9 + 4,3 + 10 %
18	Труба PP-R, армированная стекловолокном, PN20 Ø20×2,8 (Т3**)	ГОСТ 32415-2013		выбор заказчика	м	12	0,15	8,4 + 2,5 + 10 %
19	Труба канализационная ПП Ø50 (К1)	ГОСТ 32414-2013		выбор заказчика	м	13		9,6 + 2,0 + 10 %
20	Труба канализационная ПП Ø110 (К1)	ГОСТ 32414-2013		выбор заказчика	м	1,5		0,8 + 0,2 + 10 %
	Фасонные части и выводы							
21	Отвод канализационный ПП 45° Ø50	ГОСТ 32414-2013		выбор заказчика	шт	20		2 шт. на поворот
22	Отвод канализационный ПП 45° Ø110	ГОСТ 32414-2013		выбор заказчика	шт	6		2 шт. на поворот
23	Тройник канализационный ПП 45° (врезки ветвей)	ГОСТ 32414-2013		выбор заказчика	шт	5		
24	Ревизия канализационная ПП (после поворота трассы)	ГОСТ 32414-2013		выбор заказчика	шт	8		доступ сохранить
25	Фитинги PP-R Ø20: тройники, угольники 90° (ветви и повороты В1, Т3**)	ГОСТ 32415-2013		выбор заказчика	шт	29		
26	Водорозетка PP-R Ø20×½" настенная, с креплением	ГОСТ 32415-2013		выбор заказчика	шт	10		коды — лист выводов
	Узлы ввода, люки, короба							
27	Кран шаровой латунный Ду15 PN16 (отключение ввода)	аналог		выбор заказчика	шт	2		Ст В1-1, Ст Т3-1
28	Фильтр сетчатый косой Ду15	аналог		выбор заказчика	шт	2		
29	Счётчик воды крыльчатый Ду15 (ХВ, ГВ), с поверкой	аналог		выбор заказчика	шт	2		пломба УК
30	Клапан обратный Ду15	аналог		выбор заказчика	шт	2		
31	Люк ревизионный нажимной под плитку 300×400 мм	аналог		выбор заказчика	шт	3		к стоякам и арматуре
32	Звукоизоляция стояка К1 в коробе: рулонный звукоизоляционный материал ≥ 10 мм, обмотка стояка на высоту этажа	аналог		выбор заказчика	м	2,7		Ст К1-1
33	Короб К1 над полом: профиль ПН/ПС, ГКЛВ 12,5 мм под плитку	аналог		выбор заказчика	м	2,9		сечение — лист разводки

Примечания

1. Форма 1 ГОСТ 21.110-2013, ширины граф изменены по п. 4.1. «Аналог» — аналог по характеристикам: модели внести до черновых работ, привязки выводов сверить по паспортам.
2. Бытовая техника не входит (показана арматура подключения), мойка — в комплекте кухни (марка — модуля кухни, как у столяра). Длины труб — трасса листа разводки + подъёмы + 10 %.
3. Стояк К1 в коробе — звукоизоляция стояка в коробе без жёсткого контакта короба с трубой.
4. Расчёт систем водоснабжения и канализации, диаметры магистралей и подбор оборудования выполняет проектная организация.

Допущения и предложения на листе

Основа листа: размеры сняты с растрового плана заказчика без размеров: масштаб восстановлен по площадям помещений (≈ 11,8 мм на пиксель), контрольный обмер не выполнен (К-1); высота потолка 2700 мм принята: на плане заказчика её нет (К-2); толщины стен 300 / 120 мм приняты по плану заказчика, не замерены (К-1); разрешённая мощность 15 кВт принята по типовым ТУ для квартиры, ТУ заказчиком не переданы (К-4); подрайон климата не задан — принят не северный (жилые от 2,5 м) (К-9).

Знак «**» — предложение проектировщика, заказчиком не утверждено (согласовать с заказчиком): ИЗ-4: Т3.

См. лист открытых вопросов (лист 6, записи К-1, К-2, К-4; лист 7, запись К-9; лист 8, запись ИЗ-4).

						ГД-2026-007-АИ		
						Квартира 65 м²		
Изм.	Кол.уч	Лист	№ док.	Подп.	Дата	Общая площадь 65,24* м² · * размеры со скана, не замерены (реестр — л. 6–8, К-1)		
Разраб.		Кырлан А.С.			14.11.26	Дизайн-проект интерьера	Стадия: РП	Лист: 47 / Листов: 117
Пров.								
ГИП								
Н. контр.						**Спецификация сантехнического оборудования** М б/м	**Кырлан Александр Сергеевич**	
Утв.								

Техническое задание на подбор светильников

ПРЕДВАРИТЕЛЬНО · не для производства работ · открыто пунктов: 14 (реестр — л. 6–8)

Параметры для подбора: светильники, ленты и блоки питания, слои света · б/м

Параметры светильников для подбора

Поз.	Марки	Наименование	Установка	Кол.	P, Вт	Σ P, Вт	Ф, лм	Тц, К	Ra	Угол, °	IP	Дим.	Слой	Группа	Пом.
1	Св16	Потолочный накладной	на потолке, засветка стены	1	10	10	900	3000	90	—	20	—	общий	L6	1
2	Св1	Потолочный накладной	на потолке	1	36	36	3200	2700	90	—	20	—	общий	L2	2
3	Св5**	Трековая система	на потолке	2	12	24	900	2700	90	—	20	—	общий	L2	2
4	Св2, Св3	Настенный (бра)	на стене, H=1300	2	4	8	250	2700	90	—	20	—	рабочий	L8	2
5	Св4	Подвесной	подвес	1	24	24	2400	3000	90	—	20	—	общий	L1	3
6	Св6	Потолочный накладной	на потолке	1	18	18	1800	3000	90	—	20	—	общий	L1	3
7	Св7	Потолочный накладной	на потолке	1	12	12	1100	3000	90	—	20	—	общий	L1	3
8	Св8	Потолочный накладной	на потолке	1	12	12	1000	4000	90	—	20	—	общий	L1	3
9	Св9	Линейный настенный	под верхними шкафами, H=1400	1	18	18	1300	3000	90	—	20	—	рабочий	L6	3
10	Св10–Св12	Встраиваемый точечный	в ГКЛ, корпус ≤ 70 мм	3	9	27	800	3000	90	—	20	—	общий	L3	4, 5
11	Св13	Встраиваемый точечный	в ГКЛ, корпус ≤ 70 мм	1	6	6	500	3000	90	—	20	—	общий	L4	6
12	Св14	Встраиваемый точечный	в ГКЛ, корпус ≤ 70 мм	1	9	9	700	3000	90	—	44	—	общий	L4	7
13	Св15	Настенный (бра)	над зеркалом, H=1900	1	6	6	400	3000	90	—	44	—	рабочий	L4	7
14	Св26	Потолочный накладной	на потолке	1	9	9	600	3000	90	—	20	—	общий	L3	8
15	Св17–Св22	Встраиваемый точечный	в ГКЛ, корпус ≤ 70 мм	6	12	72	1050	2700	90	—	20	—	общий	L7	9
16	Св23	Лента светодиодная 24 В	в карнизе короба, профиль с рассеивателем	13,8 м	9,6/м	132,3	900/м	2700	90	—	20	да	акцентный	L8	9
17	Св24, Св25	Настенный (бра)	на стене, H=1500	2	6	12	400	2700	90	60	20	—	рабочий	L9	9
		Итого		**26 шт + 13,8 м**		**435,3**									

LED-ленты, линейные светильники и блоки питания

Марка	Пом.	L, м	U, В	Вт/м	Σ P, Вт	БП	P БП, Вт	Загр., %	Питание	Доступ к БП
Св5**	2	0,8	24	—	24	БП2	60	40	встроенный ввод	H=2300
—	3	2,5	24	—	18	БП1	60	30	встроенный ввод	H=2300
Св23	9	13,8	24	9,6	132,3	БП3	200	66	с двух концов	люк 300×300 в коробе потолка ПТ3

Слои света

общий — равномерный свет помещения, по норме освещённости

рабочий — местный свет задачи: столешница, зеркало, чтение у кровати

акцентный — подсветка потолка, стен и ниш; не входит в поток общего света

Слои света по помещениям

Пом.	Помещение	Слои света — группы включения (марки — в спецификации)	Σ P, Вт
1	Гардеробная	общий — L6	10
2	Спальня	общий — L2; рабочий — L8	68
3	Кухня-гостиная	общий — L1; рабочий — L6	84
4	Прихожая	общий — L3	9
5	Коридор	общий — L3	18
6	Санузел	общий — L4	6
7	Ванная	общий — L4; рабочий — L4	15
8	Кладовая	общий — L3	9
9	Детская	общий — L7; рабочий — L9; акцентный — L8	216,3

Допущения и предложения на листе

Основа листа: размеры сняты с растрового плана заказчика без размеров: масштаб восстановлен по площадям помещений (≈ 11,8 мм на пиксель), контрольный обмер не выполнен (К-1); высота потолка 2700 мм принята: на плане заказчика её нет (К-2); толщины стен 300 / 120 мм приняты по плану заказчика, не замерены (К-1); разрешённая мощность 15 кВт принята по типовым ТУ для квартиры, ТУ заказчиком не переданы (К-4); подрайон климата не задан — принят не северный (жилые от 2,5 м) (К-9).

Знак «**» — предложение проектировщика, заказчиком не утверждено (согласовать с заказчиком): Св5 — трековая система 2 × 900 лм: светильник добавлен проектировщиком, поток принят до нормы освещённости, модель и паспорт не выбраны.

См. лист открытых вопросов (лист 6, записи К-1, К-2, К-4; лист 7, запись К-9).

Примечания

1. Позиции и марки Св — те же, что на плане освещения (лист 30) и в ведомости светильников (лист 32); группы L — по плану выключателей (лист 31).
2. Модели светильников не выбраны: лист — техническое задание на подбор. Модель по строке таблицы: поток, Тц, Ra, угол, IP и регулировка яркости не хуже указанных, мощность не больше; встраиваемые — под глубину короба (графа «Установка»). IP 20 — сухие помещения. После выбора моделей (артикул, производитель) лист выпускается как «Спецификация светильников».
3. Длина LED-ленты в карнизе — по линии карниза плана потолков (лист 49); Σ P = Вт/м × длина. Блок питания загружен не больше чем на 80 %; лента 24 В длиннее 10 м питается с двух концов; доступ к блоку питания — люк ревизии 300×300 мм или место, указанное в таблице.
4. В пом. 9 свет включается клавишами групп — лист 31.
5. Мощность и поток в таблице — требования к подбору (поток не меньше, мощность не больше указанных); после выбора модели — по её паспорту, Σ P — установленная мощность освещения. Оценка освещённости — на плане освещения; это не светотехнический расчёт.

Изм.	Кол.уч	Лист	№ док.	Подп.	Дата
Разраб.		Кырлан А.С.			14.11.26
Пров.					
ГИП					
Н. контр.					
Утв.					

ГД-2026-007-АИ

Квартира 65 м²

Общая площадь 65,24* м² · * размеры со скана, не замерены (реестр — л. 6–8, К-1)

Дизайн-проект интерьера	Стадия	Лист	Листов
	РП	48	117

Техническое задание на подбор светильников

М б/м

Кырлан Александр Сергеевич

выпуск 14.11.2026 № 9cc0b98f36 · стр. 53 из 139

06

Потолки и ГКЛ-конструкции


Кырлан Александр Сергеевич

выпуск 14.11.2026 № 9cc0b98f36 · стр. 54 из 139

План потолков

Уровни и марки потолков, короба с подсветкой, ниши под шторы, люки, вырезы · отметки низа от ±0,000 чистого пола · размеры в мм

ПРЕДВАРИТЕЛЬНО · не для производства работ · открыто пунктов: 14 (реестр — л. 6–8)

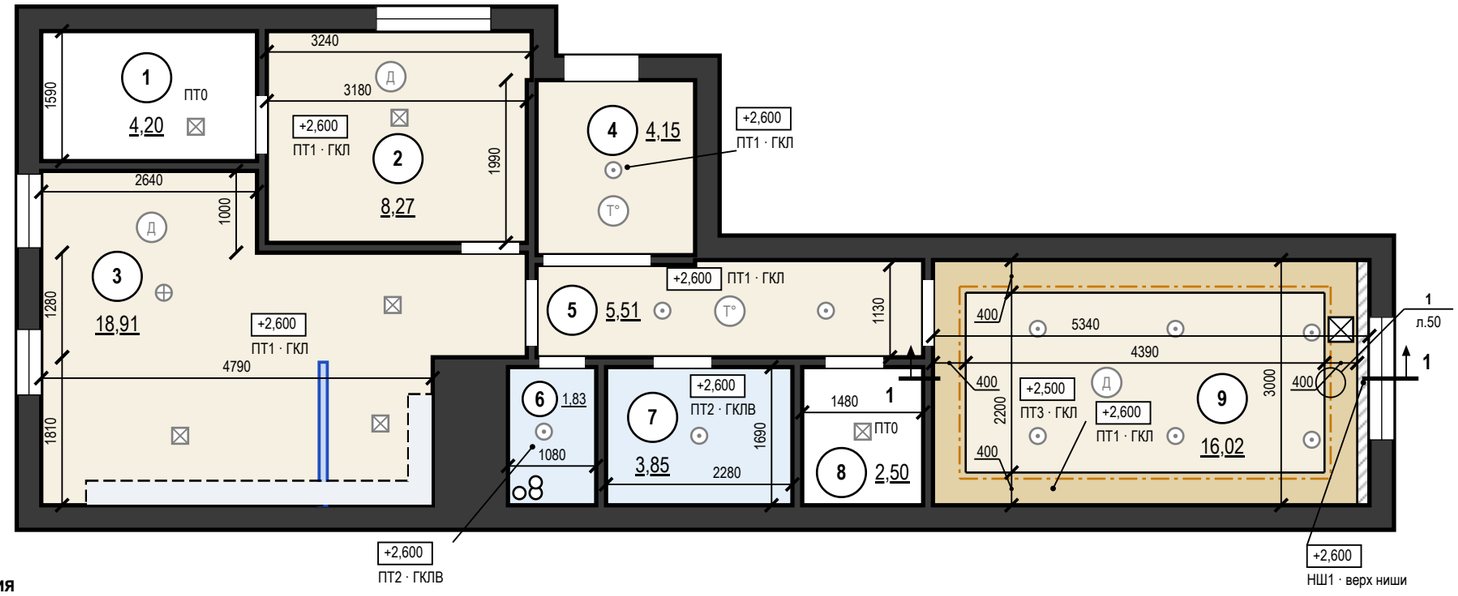

Ведомость потолков

Пом.	Марка	Конструкция	Низ / верх ниши	S, м²	Q
1, 8	ПТ0	Существующий потолок, окраска	+2,700	6,70	
2	ПТ1	ГКЛ П113	+2,600	8,27	Q3
3	ПТ1	То же	+2,600	18,91	Q3
4	ПТ1	То же	+2,600	4,15	Q3
5	ПТ1	То же	+2,600	5,51	Q3
6	ПТ2	ГКЛВ П113	+2,600	1,83	Q3
7	ПТ2	То же	+2,600	3,85	Q3
9	ПТ3	ГКЛ П113, короб LED	+2,500	5,91	Q3
9	ПТ1	ГКЛ П113	+2,600	9,66	Q3
9	НШ1	ниша под шторы 150×100	+2,600	0,45	
		Итого		**65,24**	

Ведомость вырезов и закладных в потолке

Марка	Устройство	Кол.	Пом.
	Светильник встраиваемый (марки — план освещения)	11	4, 5, 6, 7, 9
	Светильник накладной (марки — план освещения)	6	1, 2, 3, 8
	Светильник подвесной (марки — план освещения)	1	3
ИП2	Извещатель дымовой	3	2, 3, 9
ИП3**, ИП4**	Извещатель тепловой	2	4, 5
	Люк ревизии 300×300	1	9

Условные обозначения

- ПТ1 — ГКЛ по каркасу П113, низ +2,600
- ПТ2 — ГКЛВ по каркасу П113, низ +2,600
- ПТ3 — ГКЛ по каркасу П113, низ +2,500, пояс-короб с карнизом LED
- ПТ0 — существующий потолок, окраска, без подвесного потолка, низ +2,700
- НШ1 — ниша под шторы 150×100, верх +2,600
- граница уровней потолка (перепад)
- LED-лента в нише подсветки (карниз короба, ниша фигуры)
- стояк: К1 — канализация, В1 — ХВС, Т3 — ГВС
- люк ревизии в потолке 300×300 мм (доступ к БП LED)
- светильник накладной — подложка с плана освещения
- светильник подвесной — подложка с плана освещения
- светильник встраиваемый — подложка с плана освещения
- Д — извещатель дымовой на потолке — подложка
- Т° — извещатель тепловой на потолке — подложка
- короб воздуховода вытяжки ГКЛ (трасса — план вентиляции)
- линия разреза у стен помещения, стрелка — направление взгляда
- место узла: номер узла на полке, под полкой — лист
- +2,600 — отметка низа потолка, м (у ниши под шторы — верх ниши); под ней марка потолка
- новое — возводится по проекту (синим)
- 1 — номер помещения, площадь м²

Примечания

1. За отметку ±0,000 принят уровень чистого пола сухих помещений (готовое покрытие), а не существующего пола; пол пом. 6, 7 — −0,015; верх плиты перекрытия −0,064 — расчётный по пирогу пола, не замерен; существующий пол снимается до плиты, его отметка не замерена. Отметки в прямоугольниках — низ потолка; низ перекрытия +2,700. Марка потолка — одна конструкция и отметка на весь альбом.
2. Размеры помещений в свету (ширина × длина, мм), не поместившиеся на плане: пом. 1 — 2640 × 1590; пом. 2 — 3240 × 600, 3180 × 1990; пом. 3 — 2640 × 1000, 5940 × 1280, 4790 × 1810; пом. 4 — 1940 × 2140; пом. 5 — 2790 × 60, 4730 × 1130; пом. 6 — 1080 × 1690; пом. 8 — 1480 × 1690.
3. Потолки ГКЛ — каркасная система П113: подвесы через 1000 (с запасом: СП 163, табл. 14 — до 1100 при 0,15 кН/м²), несущие профили через 500, основные через 1200 мм; листы — поперёк несущих профилей. В помещениях 6, 7 — ГКЛВ на оцинкованном каркасе.
4. Нижний уровень — пояс-короб по периметру шириной 400 мм, верхний — поле внутри пояса: пом. 9.
5. LED-лента в алюминиевом профиле посередине карниза короба шириной 400 мм (узел 1, лист 50); длина по плану: пом. 9 — 13,8 м (в плане освещения 13,8).
6. Ниши под шторы 150×100 мм — на всю длину стены с окном; карниз — на закладной до обшивки (узел 2, лист 50).
7. Примыкание к стенам: теневой шов 15 мм, техзазор 3 мм — пом. 2, 3, 4, 5, 9, по стенам, выровненным штукатуркой (узел 1); пом. 6, 7 — разделительная лента.
8. Светильники и потолочные устройства — подложка с планов освещения, слаботочных систем и вентиляции (положение — по ним); вырезы и закладные — по ведомости на листе, до обшивки; отверстия не совмещать с профилями, глубина корпуса светильника до 70 мм.
9. Разрезы 1–1 — на листе 50; высоты мебели и дверных блоков сверены с низом потолка в разрезах.
10. Узлы по выноскам на плане: узлы 1, 2 — лист 50; сечения М 1:10 по помещениям — лист 51.
11. Шпаклевание ГКЛ и условия приёмки — Q3: рассеянный дневной свет, осмотр с 2 м; боковой свет не оценивается.
12. Пом. 3: короб воздуховода кухонной вытяжки ГКЛ 300×200 мм (ширина от стены × высота), низ +2,500, длина 5,00 м — по трассе плана вентиляции, вдоль стен до входа в канал под воздуховод Ø125; каркас ПН 28×27 по стене и плите, ПП 60×27, лист ГКЛ 12,5.
13. Люки ревизии 300×300 мм — по центру блоков питания LED (БП3; координаты — план освещения).
14. Сечения потолков М 1:10: пом. 9 — 9.1, 9.2 (лист 51).

1000 мм · печать 1:1

Допущения и предложения на листе

Основа листа: размеры сняты с растрового плана заказчика без размеров: масштаб восстановлен по площадям помещений (≈ 11,8 мм на пиксель), контрольный обмер не выполнен (К-1); высота потолка 2700 мм принята: на плане заказчика её нет (К-2); толщины стен 300 / 120 мм приняты по плану заказчика, не замерены (К-1); разрешённая мощность 15 кВт принята по типовым ТУ для квартиры, ТУ заказчиком не переданы (К-4); подрайон климата не задан — принят не северный (жилые от 2,5 м) (К-9).

Знак «**» — предложение проектировщика, заказчиком не утверждено (согласовать с заказчиком): ИП3, ИП4 — прихожая / кухня квартиры — тепловой (СП 484, прил. Б, Б.4); место — центр помещения, не ближе 500 мм к светильнику.

Открытые вопросы и конфликты по листу: К-2, К-9.

См. лист открытых вопросов (лист 6, записи К-1, К-2, К-4; лист 7, запись К-9).

Изм.	Кол.уч	Лист	№ док.	Подп.	Дата
Разраб.		Кырлан А.С.			14.11.26
Пров.					
ГИП					
Н. контр.					
Утв.					

ГД-2026-007-АИ

Квартира 65 м²

Общая площадь 65,24* м² · * размеры со скана, не замерены (реестр — л. 6–8, К-1)

Дизайн-проект интерьера

Стадия	Лист	Листов
РП	49	117

План потолков

М 1:75

Кырлан Александр Сергеевич


выпуск 14.11.2026 № 9cc0b98f36 · стр. 55 из 139

Разрезы и узлы потолков

Разрезы по потолкам с отметками уровней · узлы коробов и ниш · размеры в мм


Разрез 1–1 (М 1:40)

Пом. 9 Детская; линия разреза — план потолков, лист 49

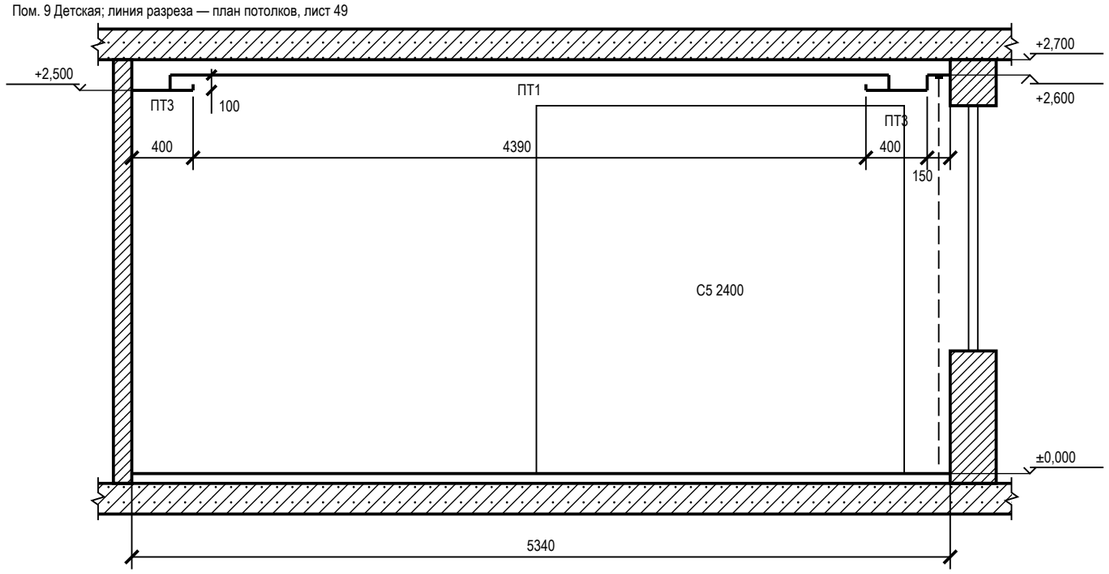

1 Короб с LED-подсветкой, теневой шов (М 1:10)


Пом. 9; карниз 150×100, щель под свет 60 мм

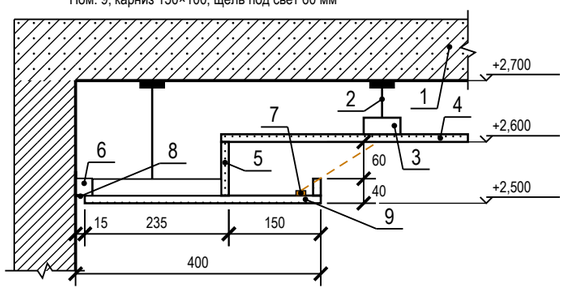

1 — плита перекрытия
2 — подвес прямой, шаг 1000 мм
3 — ПП 60×27: несущие через 500, основные через 1200 мм
4 — ГКЛ 12,5 по П113 — верхний уровень
5 — задняя стенка и бортик карниза — ГКЛ 12,5
6 — ПН 28×27 по периметру, к стене через 500 мм
7 — LED-лента в алюминиевом профиле
8 — теневой профиль: шов 15 мм, зазор 3 мм
9 — низ короба — ГКЛ 12,5 по ПП 60×27

2 Ниша под шторы (М 1:10)

Пом. 9; без подсветки; закладные под карниз — до обшивки

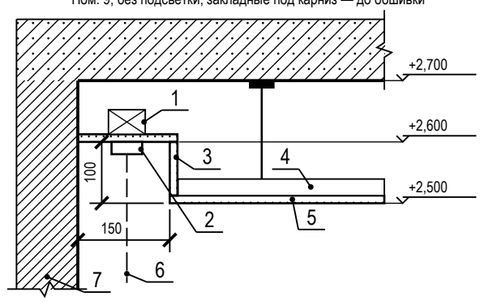

1 — закладная под карниз — брус 40×50
2 — карниз (шина), высота с верхом портьеры 80 мм
3 — стенка и потолок ниши — ГКЛ 12,5
4 — ПП 60×27 — каркас короба
5 — низ короба нижнего уровня — ГКЛ 12,5
6 — портьера
7 — стена с окном

Условные обозначения

- плита перекрытия в сечении
- стена в сечении
- потолок ГКЛ в сечении; под линией — марка потолка (план потолков)
- мебель и дверные проёмы за секущей плоскостью; число — марка и верх от чистого пола, мм
- портьера в нише под шторы

Допущения и предложения на листе

Основа листа: размеры сняты с растрового плана заказчика без размеров: масштаб восстановлен по площадям помещений (≈ 11,8 мм на пиксель), контрольный обмер не выполнен (К-1); высота потолка 2700 мм принята: на плане заказчика её нет (К-2); толщины стен 300 / 120 мм приняты по плану заказчика, не замерены (К-1); разрешённая мощность 15 кВт принята по типовым ТУ для квартиры, ТУ заказчиком не переданы (К-4); подрайон климата не задан — принят не северный (жилые от 2,5 м) (К-9).
См. лист открытых вопросов (лист 6, записи К-1, К-2, К-4; лист 7, запись К-9).

Примечания

1. Разрезы — по линиям 1–1 на плане потолков (лист 49). Отметки — от ±0,000 чистого пола, м; размеры — мм.
2. Высоты мебели и дверных блоков за секущей плоскостью сверены с низом потолка над ними: верх ниже низа короба и поля.
3. ГКЛ 12,5 мм по каркасу П113; перепад уровней и бортик карниза — ГКЛ по ПП 60×27 (узел 1 — на этом листе). Ниша под шторы — на всю длину стены с окном, карниз на закладной до обшивки (узел 2 — на этом листе).
4. Толщины плит перекрытия и пирога пола показаны условно.
5. Сечения потолков по помещениям М 1:10 (отметки помещения, профили, подвесы, крепёж, изделия) — лист 51.
6. Ведомость объёмов потолков (лист ГКЛ, профиль, подвесы, лента, блоки питания, люки) — на листе 51.

1000 мм · печать 1:1

						ГД-2026-007-АИ	
						Квартира 65 м²	
Изм.	Кол.уч	Лист	№ док.	Подп.	Дата	Общая площадь 65,24* м² · * размеры со скана, не замерены (реестр — л. 6–8, К-1)	
Разраб.		Кырлан А.С.			14.11.26	Дизайн-проект интерьера	Стадия: РП; Лист: 50; Листов: 117
Пров.							
ГИП						Разрезы и узлы потолков	Кырлан Александр Сергеевич
						М 1:40; 1:10	
Н. контр.							
Утв.							

выпуск 14.11.2026 № 9cc0b98f36 · стр. 56 из 139


Сечения потолков М 1:10

Пом. 9 · профили, подвесы, крепёж, изделия · размеры в мм

ПРЕДВАРИТЕЛЬНО · не для производства работ · открыто пунктов: 14 (реестр — л. 6–8)

Сечение 9.1. Короб с LED-подсветкой, теневой шов (М 1:10)


Пом. 9 Детская; карниз 150×100, щель под свет 60 мм

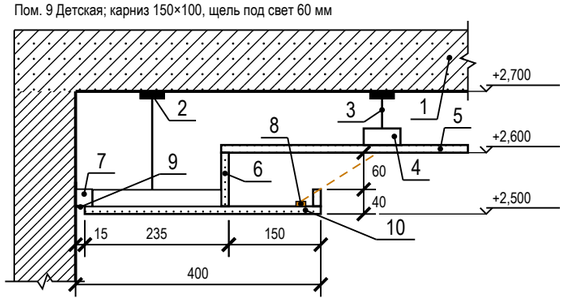

1 — плита перекрытия
2 — анкер-клин к плите — по одному на подвес
3 — подвес прямой, шаг 1000 мм
4 — ПП 60×27: несущие через 500, основные через 1200 мм; соединители одноуровневые, шурупы LN 3,5×9
5 — ГКЛ 12,5 по П113 — верхний уровень; шурупы TN 3,5×25 через 170 мм
6 — задняя стенка и бортик карниза — ГКЛ 12,5
7 — ПН 28×27 по периметру — дюбель-гвоздь через ≤ 500 мм, не менее 3 на профиль
8 — LED-лента 9,6 Вт/м, 24 В в алюминиевом профиле
9 — теневой профиль: шов 15 мм, зазор 3 мм
10 — низ короба — ГКЛ 12,5 по ПП 60×27

Сечение 9.2. Ниша под шторы (М 1:10)

Пом. 9 Детская; без подсветки; закладные под карниз — до обшивки

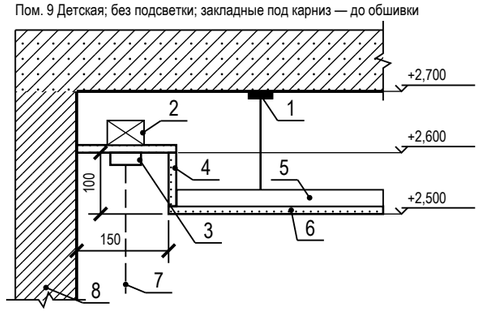

1 — анкер-клин к плите — по одному на подвес; подвес прямой, шаг 1000 мм
2 — закладная под карниз — брус 40×50
3 — карниз (шина), высота с верхом портьеры 80 мм
4 — стенка и потолок ниши — ГКЛ 12,5
5 — ПП 60×27 — каркас короба, основные через 1200 мм; соединители одноуровневые, шурупы LN 3,5×9
6 — низ короба нижнего уровня — ГКЛ 12,5; шурупы TN 3,5×25 через 170 мм
7 — портьера
8 — стена с окном

Ведомость объёмов потолков

Позиция	Ед.	Кол.	Пом.
Лист ГКЛ 12,5	м²	57,10	2, 3, 4, 5, 9
Лист ГКЛВ 12,5	м²	5,68	6, 7
Борта и карнизы (входят в площади листов выше)	м²	4,24	9
Профиль ПП 60×27	м	169,79	2, 3, 4, 5, 6, 7, 9
Профиль ПН 28×27	м	128,02	2, 3, 4, 5, 6, 7, 9
Подвес прямой	шт.	64	2, 3, 4, 5, 6, 7, 9
Анкер-клин к плите	шт.	64	2, 3, 4, 5, 6, 7, 9
Шуруп TN 3,5×25	шт.	1444	2, 3, 4, 5, 6, 7, 9
Лента армирующая для швов	м	75,34	2, 3, 4, 5, 6, 7, 9

Ведомость объёмов потолков (окончание)

Позиция	Ед.	Кол.	Пом.
Шпаклёвка для швов	кг	25,11	2, 3, 4, 5, 6, 7, 9
Грунтовка (швы)	л	6,28	2, 3, 4, 5, 6, 7, 9
Лента разделительная по периметру	м	81,88	2, 3, 4, 5, 6, 7, 9
Сплошная шпаклёвка и окраска (площадь развёртки)	м²	62,78	2, 3, 4, 5, 6, 7, 9
Лента LED	м	13,78	9
Требуемая мощность блоков питания	Вт	172	9
Установленная мощность блоков питания	Вт	200	9
Блок питания LED	шт.	1	9
Люк ревизии	шт.	1	9

Условные обозначения

— · — LED-лента в нише подсветки (карниз короба, ниша фигуры)

Допущения и предложения на листе

Основа листа: размеры сняты с растрового плана заказчика без размеров: масштаб восстановлен по площадям помещений (≈ 11,8 мм на пиксель), контрольный обмер не выполнен (К-1); высота потолка 2700 мм принята: на плане заказчика её нет (К-2); толщины стен 300 / 120 мм приняты по плану заказчика, не замерены (К-1); разрешённая мощность 15 кВт принята по типовым ТУ для квартиры, ТУ заказчиком не переданы (К-4); подрайон климата не задан — принят не северный (жилые от 2,5 м) (К-9).
См. лист открытых вопросов (лист 6, записи К-1, К-2, К-4; лист 7, запись К-9).

Примечания

1. Сечения потолков М 1:10 по помещениям с нишами LED и нишами под шторы: отметки и размеры этого помещения от ±0,000 чистого пола (м, мм). Положение — по плану потолков (лист 49): короб и ниша LED — по линиям ленты, ниша под шторы — у стены с окном; типовые узлы по группам помещений — на листе 50.
2. Крепёж: подвес прямой к плите на анкер-клине — по одному на подвес (Knauf П113); ПН к стенам — дюбель-гвоздь через ≤ 500 мм, не менее 3 на профиль (серия 1.045.9-2.08); лист 12,5 — шурупы TN 3,5×25 через 170 мм (СП 163, табл. 15); профили между собой — соединители одноуровневые, шурупы LN 3,5×9.
3. Изделие карниза, профиля LED и галтели подписано артикулом из данных; где артикул не выбран, сечение дано по габаритам из данных (ширина и глубина ниши, щель под свет), изделие подбирается по ним.
4. Ведомость объёмов — по геометрии плана потолков: Лист ГКЛ 12,5 — плоскости уровней + борта (без арочных участков); Лист ГКЛВ 12,5 — плоскости уровней + борта; Борта и карнизы — длина перепада × перепад; Профиль ПП 60×27 — S × (1/шаг несущ. + 1/шаг осн.) + стойки бортов; Профиль ПН 28×27 — периметр стен + 2 × перепады + карнизы; Подвес прямой — по раскладке: S уровня / (шаг осн. × шаг подвесов), пояс уже шага — ряд вдоль пояса, фигура — по контуру; шаг подвесов — не больше табл. 14 СП 163; Анкер-клин к плите — по одному на подвес (Knauf П113); Шуруп TN 3,5×25 — 23 шт./м² (Knauf П113, табл. 2 альбома П 11); Лента армирующая для швов — 1,2 м/м² листа (Knauf); Шпаклёвка для швов — 0,4 кг/м² листа, только швы (Knauf); Грунтовка (швы) — 0,1 л/м² листа, только швы (Knauf); Лента разделительная по периметру — периметр стен под потолком ГКЛ; Сплошная шпаклёвка и окраска (площадь развёртки) — плоскости + борта; расход — по паспорту материала (норма расхода на сплошной слой не подтверждена); Лента LED — по оси карниза и ниши фигуры (план потолков); Требуемая мощность блоков питания — Вт/м × длина × 1,3; Установленная мощность блоков питания — сумма мощностей блоков по плану освещения; Блок питания LED — блоки потолочных лент по плану освещения (БП3); Люк ревизии — план потолков; без запаса на подрезку (при закупке листа: ×1,075 при S > 20 м², ×1,175 — 10–20 м², ×1,275 — < 10 м²).

1000 мм · печать 1:1

Изм.	Кол.уч	Лист	№ док.	Подп.	Дата
Разраб.		Кырлан А.С.			14.11.26
Пров.					
ГИП					
Н. контр.					
Утв.					

ГД-2026-007-АИ

Квартира 65 м²

Общая площадь 65,24* м² · * размеры со скана, не замерены (реестр — л. 6–8, К-1)

Дизайн-проект интерьера

Стадия	Лист	Листов
РП	51	117

Сечения потолков М 1:10

М 1:10

Кырлан Александр Сергеевич


выпуск 14.11.2026 № 9cc0b98f36 · стр. 57 из 139

Раскладка плитки. Планы полов


Раскладка от чистовых размеров · размеры в мм · отметки от ±0,000

ПРЕДВАРИТЕЛЬНО · не для производства работ · открыто пунктов: 14 (реестр — л. 6–8)

Фрагмент 1. Санузел (пом. 6). Пол 600×1200, шов 2 мм (М 1:20)

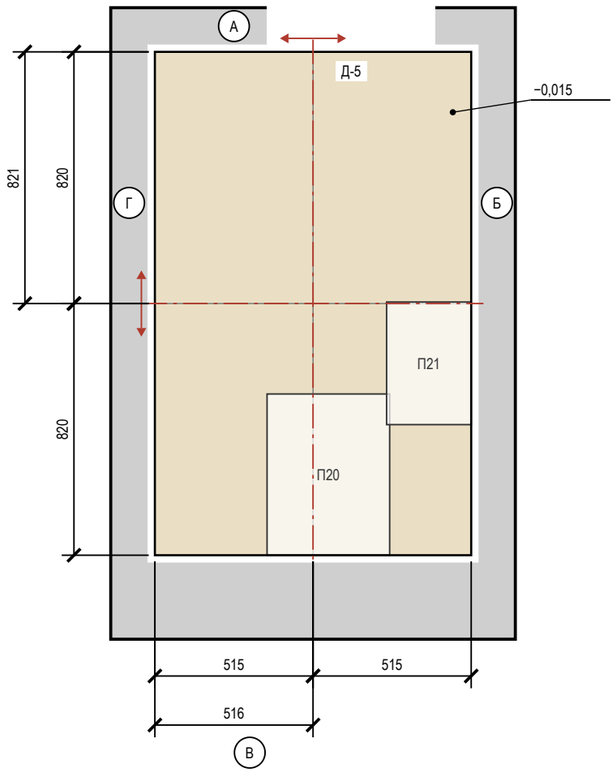

Фрагмент 2. Ванная (пом. 7). Пол 600×1200, шов 2 мм (М 1:20)

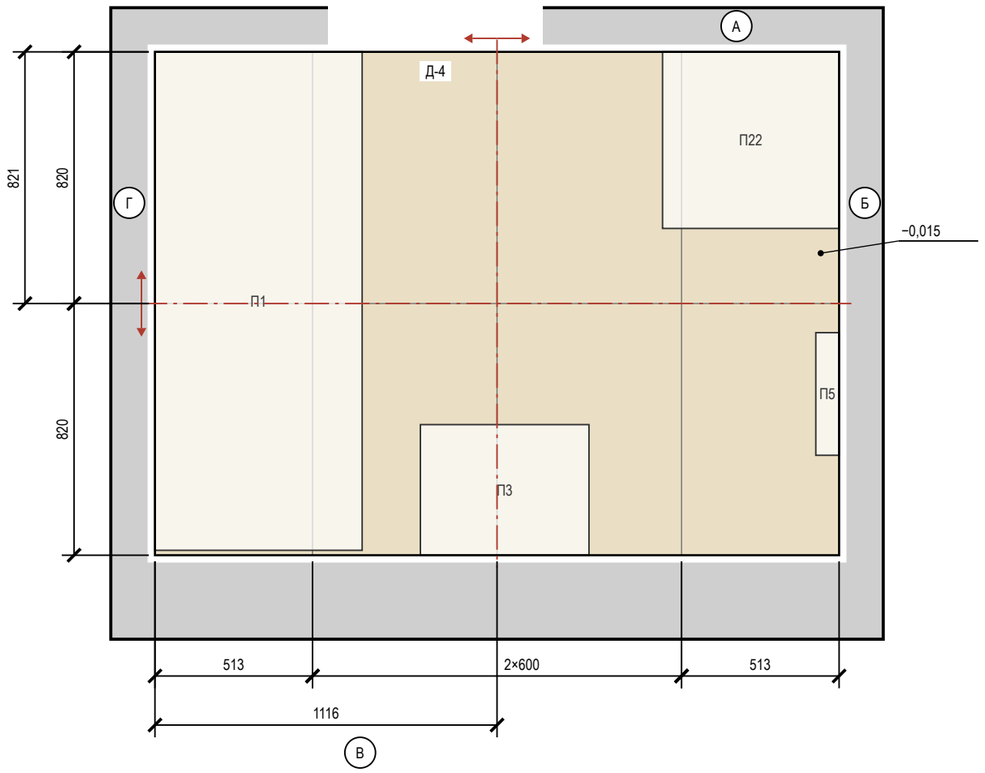

Условные обозначения

- плитка целая; тонкая линия — шов
- плитка с подрезкой (размер — на цепочке)
- ось старта; стрелки — направление укладки
- сантехприбор: габарит, высота по практике
- отметка чистого пола на полке выноски, м
- (А) обозначение стены А–Г (как на развёртках)

Ведомость плитки

Помещение, поверхность	Плитка, код	Формат	Шов	S, м²	Целых	Подр.	С запасом
Санузел, пол	SG501600R	600×1200	2	1,83	0	4	5
Санузел, стены А–Г	610010001195	1200×600	2	13,33	0	30	34
Ванная, пол	SG501600R	600×1200	2	3,85	0	8	9
Ванная, стены А–Г	610010001195	1200×600	2	19,29	0	40	44
Прихожая, пол	SG501600R	600×1200	2	4,15	0	8	9
Коридор, пол	SG501600R	600×1200	2	5,51	0	8	9
Итого 600×1200				**47,97**	**0**	**98**	**110**

Ведомость материалов

Материал	Класс, код	Норма расхода	Кол-во
Затирка	класс не задан	(a+b)/ab·шов·t·1,6	3,7 кг
Клей	C2 S1	1,2 кг/м²·мм, слой 5	36 кг (2 меш.)
Клей	C2	1,2 кг/м²·мм, слой 5	271 кг (11 меш.)
Гидроизоляция	обмазочная, 2 слоя: пол, стены по периметру и зоны замачивания	по ТУ	14,8 м²
Демпф. лента	по периметру пола из плитки		27,0 м

Примечания

1. Раскладка от чистовых размеров: стены санузлов теряют 10 + 5 + 9 = 24 мм на сторону (штукатурка, клей, плитка); подрезки — чистые, без шва.
2. Старт — от центра помещения (штрихпунктир, стрелки — направление укладки); размер старта — от чистовых стен Г и А.
3. Раскладка пола «Прихожая» и пола «Коридор» — на листе «Раскладка плитки. Прихожая. Коридор».
4. Калибр партии не задан — до укладки замерить (рабочий размер W, ГОСТ 13996-2019) и пересчитать подрезки.
5. Количество: целые по раскладке + по одной на подрезку, запас 10 %; один артикул — одна партия и тон. Исключены поддон, короб, проёмы и места за коробом; S — по чистым граням, как в ведомости отделки.
6. Клей C2 S1; C2 (ГОСТ Р 56387-2018), затирка класс не задан; расход — по ТУ выбранной марки.
7. Гидроизоляция: пол и стены 200 мм от ЧП; над ванной — до 2000 и 300 мм за борт (пом. 7) (см. развёртки); акт скрытых работ, пролив 24 ч.
8. Отметка чистого пола −0,015, порог 15 мм; стык с соседним покрытием — по оси полотна двери.

Допущения и предложения на листе

Основа листа: размеры сняты с растрового плана заказчика без размеров: масштаб восстановлен по площадям помещений (≈ 11,8 мм на пиксель), контрольный обмер не выполнен (К-1); высота потолка 2700 мм принята: на плане заказчика её нет (К-2); толщины стен 300 / 120 мм приняты по плану заказчика, не замерены (К-1); разрешённая мощность 15 кВт принята по типовым ТУ для квартиры, ТУ заказчиком не переданы (К-4); подрайон климата не задан — принят не северный (жилые от 2,5 м) (К-9).
См. лист открытых вопросов (лист 6, записи К-1, К-2, К-4; лист 7, запись К-9).

1000 мм · печать 1:1

Изм.	Кол.уч	Лист	№ док.	Подп.	Дата
Разраб.		Кырлан А.С.			14.11.26
Пров.					
ГИП					
Н. контр.					
Утв.					

ГД-2026-007-АИ

Квартира 65 м²

Общая площадь 65,24* м² · * размеры со скана, не замерены (реестр — л. 6–8, К-1)

Дизайн-проект интерьера	Стадия	Лист	Листов
	РП	52	117

Раскладка плитки. Планы полов

М 1:20

Кырлан Александр Сергеевич


выпуск 14.11.2026 № 9cc0b98f36 · стр. 58 из 139

Раскладка плитки. Прихожая. Коридор


Раскладка от чистовых размеров · размеры в мм · высоты фартука от чистого пола

ПРЕДВАРИТЕЛЬНО · не для производства работ · открыто пунктов: 14 (реестр — л. 6–8)

Фрагмент 1. Прихожая (пом. 4). Пол 600×1200, шов 2 мм (М 1:25)

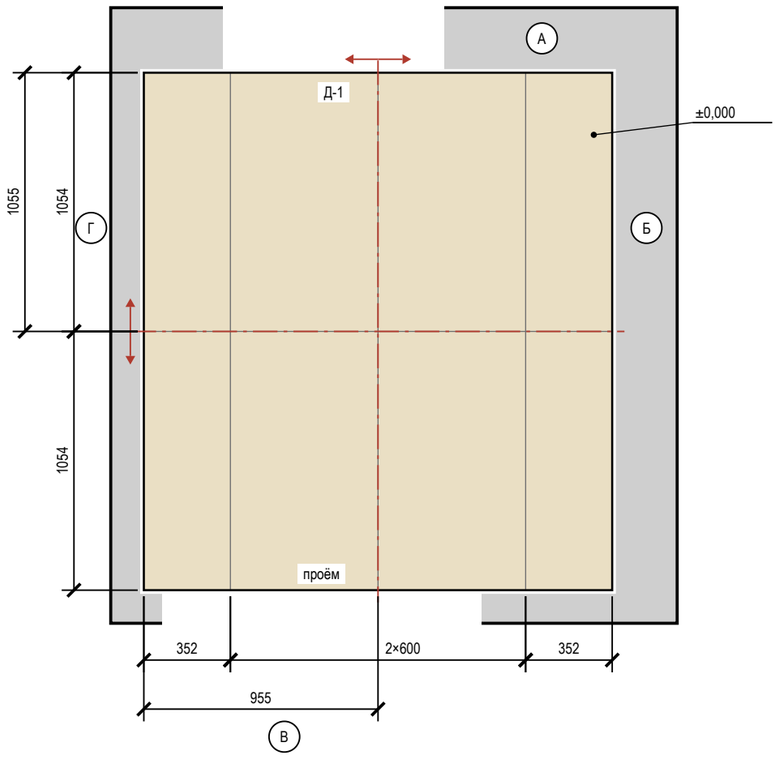

Фрагмент 2. Коридор (пом. 5). Пол 600×1200, шов 2 мм (М 1:25)

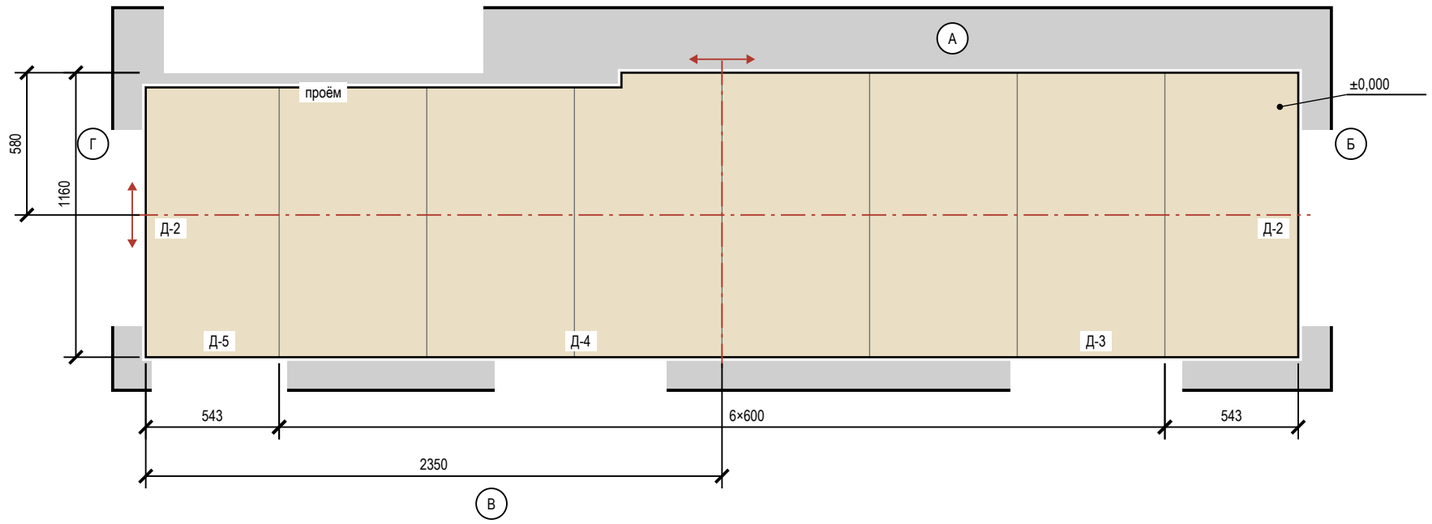

Условные обозначения

- плитка целая; тонкая линия — шов
- плитка с подрезкой (размер — на цепочке)
- ось старта; стрелки — направление укладки
- отметка чистого пола на полке выноски, м
- (А) обозначение стены А–Г (как на развёртках)

Подсчёт плитки

Поверхность	Формат	S, м²	Целых	Подр.	С запасом
Прихожая, пол	600×1200	4,15	0	8	9
Коридор, пол	600×1200	5,51	0	8	9

Примечания

1. Прихожая: керамогранит 600×1200, длинная сторона — вдоль стен Б и Г, шов 2 мм, прямая раскладка от центра. Стены окрашены: раскладка от чистового контура минус штукатурка и шпаклёвка 15 мм на сторону (принято); подрезки 352 / 1054 мм, срез — под плинтус.
2. Прихожая: деформационный зазор по периметру 8–10 мм под плинтусом; в проёмах — стык с соседним покрытием по оси полотна двери. Клей С2, затирка класс не задан.
3. Коридор: керамогранит 600×1200, длинная сторона — вдоль стен Б и Г, шов 2 мм, прямая раскладка от центра. Стены окрашены: раскладка от чистового контура минус штукатурка и шпаклёвка 15 мм на сторону (принято); подрезки 543 / 1160 мм, срез — под плинтус.
4. Коридор: деформационный зазор по периметру 8–10 мм под плинтусом; в проёмах — стык с соседним покрытием по оси полотна двери. Клей С2, затирка класс не задан.
5. Клей, затирка и итог по форматам — в ведомостях листа «Раскладка плитки. Планы полов».

Допущения и предложения на листе

Основа листа: размеры сняты с растрового плана заказчика без размеров: масштаб восстановлен по площадям помещений (≈ 11,8 мм на пиксель), контрольный обмер не выполнен (К-1); высота потолка 2700 мм принята: на плане заказчика её нет (К-2); толщины стен 300 / 120 мм приняты по плану заказчика, не замерены (К-1); разрешённая мощность 15 кВт принята по типовым ТУ для квартиры, ТУ заказчиком не переданы (К-4); подрайон климата не задан — принят не северный (жилые от 2,5 м) (К-9).
См. лист открытых вопросов (лист 6, записи К-1, К-2, К-4; лист 7, запись К-9).

1000 мм · печать 1:1

Изм.	Кол.уч	Лист	№ док.	Подп.	Дата
Разраб.		Кырлан А.С.			14.11.26
Пров.					
ГИП					
Н. контр.					
Утв.					

ГД-2026-007-АИ

Квартира 65 м²

Общая площадь 65,24* м² · * размеры со скана, не замерены (реестр — л. 6–8, К-1)

Дизайн-проект интерьера

Стадия	Лист	Листов
РП	53	117

Раскладка плитки. Прихожая. Коридор

М 1:25


Кырлан Александр Сергеевич

выпуск 14.11.2026 № 9cc0b98f36 · стр. 59 из 139

Раскладка плитки. Санузел. Развёртки стен

ПРЕДВАРИТЕЛЬНО · не для производства работ · открыто пунктов: 14 (реестр — л. 6–8)

Пом. 6 · вид изнутри помещения · размеры в мм · высоты от чистого пола, отметки от ±0,000

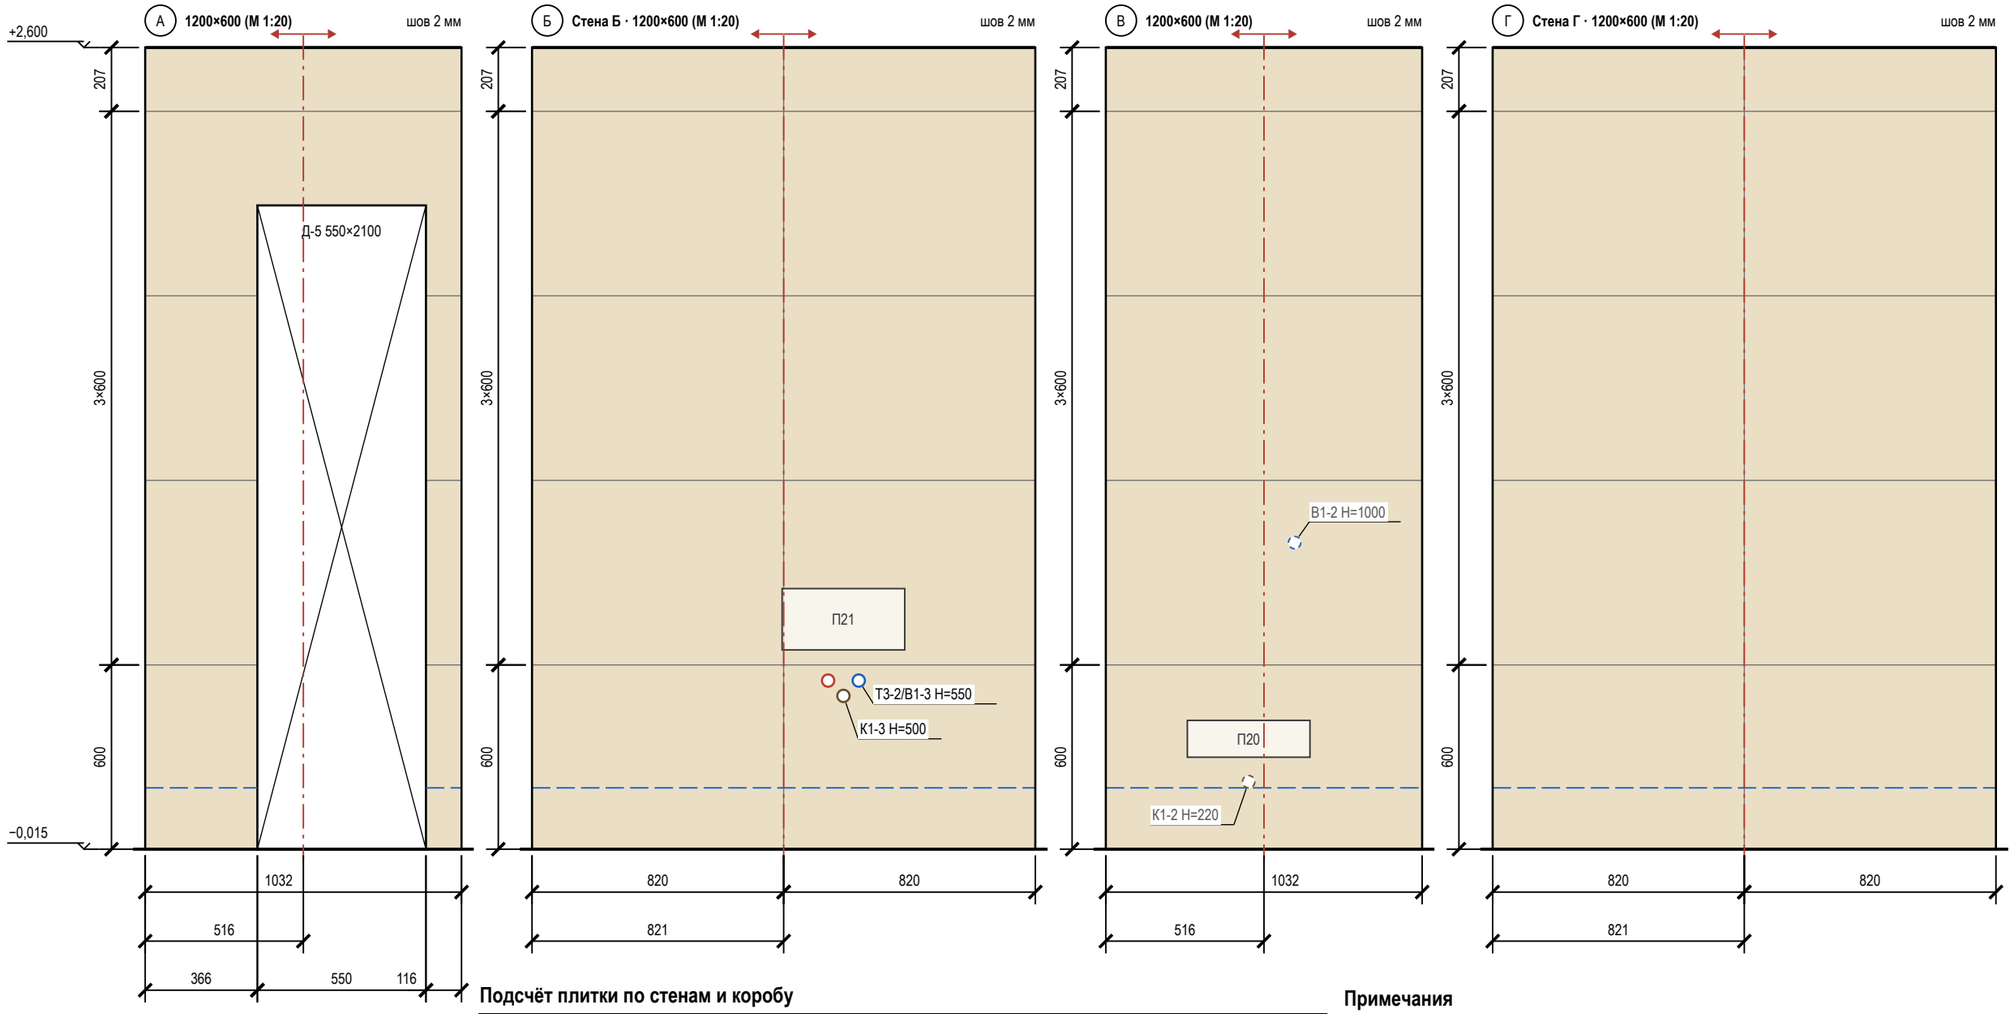

Подсчёт плитки по стенам и коробу

Поверхность	L × H, мм	S, м²	Целых	Подр.	С запасом	Подрезки: край / верх, мм
стена А	1032 × 2615	1,67	0	5	6	1032; 207
стена Б	1642 × 2615	4,42	0	10	11	820 / 820; 207
стена В	1032 × 2615	2,82	0	5	6	1032; 207
стена Г	1642 × 2615	4,42	0	10	11	820 / 820; 207
Итого		**13,33**	**0**	**30**	**34**	

Примечания

1. Вид изнутри, стены по часовой стрелке А → Г. Высоты — от чистого пола (−0,015), отметки — от ±0,000. Раскладка от чистовых размеров (штукатурка 10 + клей 5 + плитка 9 мм), подрезки чистые; старт — от оси стены, ряды от пола целыми.
2. Облицовка до потолка (+2,600).
3. Открытые выводы и электроточки — на шве или в центре плитки (допуск 10 мм; плитка от 900 мм по высоте — на шве или не ближе 60 мм к нему).
4. Выводы ВК стоят по оси прибора и с прибором не двигаются — привязки по «Плану выводов сантехники» без сдвига; вне сетки (Т3-2/В1-3, К1-3) — отверстие в плитке коронкой по той же привязке, плитку не сдвигать.
5. Выводы — по «Плану выводов сантехники», электроточки — по ЭОМ, «*» — высота по практике; за приборами и в коробе (В1-2, К1-2) — штриховым кольцом.
6. Гидроизоляция: 200 мм от ЧП по периметру; углы — лентой; акт скрытых работ, пролив.

Условные обозначения

- плитка целая; тонкая линия — шов
- плитка с подрезкой (размер — на цепочке)
- ось старта; стрелки — направление укладки
- верх гидроизоляции: 200 от ЧП, в мокрой зоне — «до …»
- проём — не облицовывается
- сантехприбор: габарит, высота по практике
- вывод В1 (код — в ведомости привязок)
- вывод Т3 (код — в ведомости привязок)
- вывод К1 (код — в ведомости привязок)
- вывод за прибором / в коробе (не на сетке)
- отметка уровня, м: ±0,000 — чистый пол жилых помещений
- низ потолка; серая полоса — стена без плитки
- (А) обозначение стены А–Г (как на развёртках)

1000 мм · печать 1:1

Допущения и предложения на листе. См. лист открытых вопросов (листы 6–8).

Изм.	Кол.уч	Лист	№ док.	Подп.	Дата
Разраб.		Кырлан А.С.			14.11.26
Пров.					
ГИП					
Н. контр.					
Утв.					

ГД-2026-007-АИ

Квартира 65 м²

Общая площадь 65,24* м² · * размеры со скана, не замерены (реестр — л. 6–8, К-1)

Дизайн-проект интерьера

Стадия	Лист	Листов
РП	54	117

Раскладка плитки. Санузел. Развёртки стен

М 1:20


Кырлан Александр Сергеевич

выпуск 14.11.2026 № 9cc0b98f36 · стр. 60 из 139

Раскладка плитки. Ванная. Развёртки стен

ПРЕДВАРИТЕЛЬНО · не для производства работ · открыто пунктов: 14 (реестр — л. 6–8)

Пом. 7 · вид изнутри помещения · размеры в мм · высоты от чистого пола, отметки от ±0,000

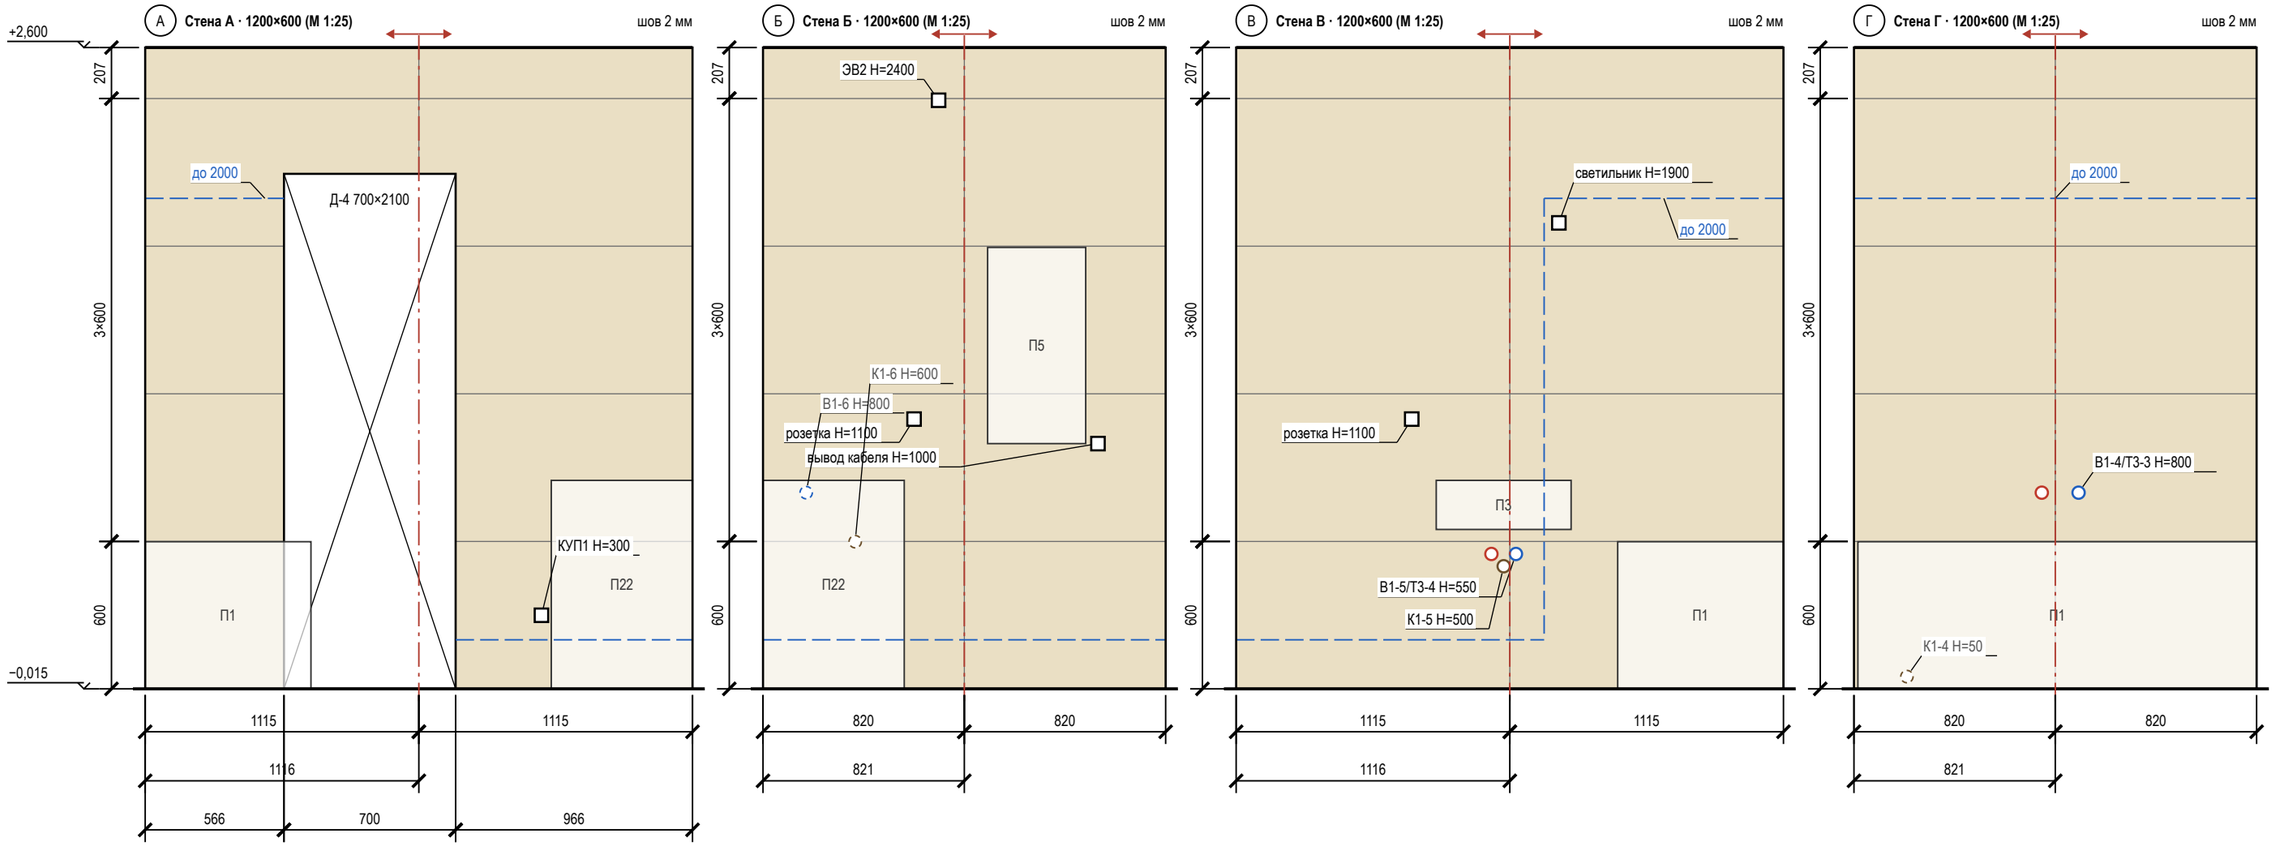

Подсчёт плитки по стенам и коробу

Поверхность	L × H, мм	S, м²	Целых	Подр.	С запасом	Подрезки: край / верх, мм
стена А	2232 × 2615	4,49	0	10	11	1115 / 1115; 207
стена Б	1642 × 2615	4,42	0	10	11	820 / 820; 207
стена В	2232 × 2615	5,96	0	10	11	1115 / 1115; 207
стена Г	1642 × 2615	4,42	0	10	11	820 / 820; 207
Итого		**19,29**	**0**	**40**	**44**	

Сдвиг точек под раскладку

Точка (ВК, ЭОМ)	Стена	Проект: от угла / Н	Под раскладку: от угла / Н	Сдвиг, мм
вывод кабеля	Б	1366 / 1000	1366 / 902	Н −98
розетка	Б	616 / 1100	616 / 1203	Н +103
розетка	В	716 / 1100	716 / 1203	Н +103
светильник	В	1316 / 1900	1316 / 1805	Н −95

Примечания

1. Вид изнутри, стены по часовой стрелке А → Г. Высоты — от чистого пола (−0,015), отметки — от ±0,000. Раскладка от чистовых размеров (штукатурка 10 + клей 5 + плитка 9 мм), подрезки чистые; старт — от оси стены, ряды от пола целыми.
2. Облицовка до потолка (+2,600).
3. Точки из таблицы сдвигов переносятся до черновой разводки (ЭОМ — по тем же числам).
4. Выводы ВК стоят по оси прибора и с прибором не двигаются — привязки по «Плану выводов сантехники» без сдвига; вне сетки (В1-5/Т3-4, К1-5, В1-4/Т3-3) отверстие в плитке коронкой по той же привязке, плитку не сдвигать.
5. Выводы — по «Плану выводов сантехники», электроточки — по ЭОМ, «*» — высота по практике; за приборами и в коробе (В1-6, К1-6, К1-4) — штриховым кольцом.
6. Гидроизоляция: 200 мм от ЧП по периметру; над ванной — до 2000 и 300 мм за борт (СП 29.13330.2011, п. 7.2 — на высоту замачивания); углы — лентой; акт скрытых работ, пролив.

Условные обозначения

- плитка целая; тонкая линия — шов
- плитка с подрезкой (размер — на цепочке)
- ось старта; стрелки — направление укладки
- верх гидроизоляции: 200 от ЧП, в мокрой зоне — «до …»
- проём — не облицовывается
- сантехприбор: габарит, высота по практике
- вывод В1 (код — в ведомости привязок)
- вывод Т3 (код — в ведомости привязок)
- вывод К1 (код — в ведомости привязок)
- вывод за прибором / в коробе (не на сетке)
- электроточка: марка и Н — по листам ЭОМ
- отметка уровня, м: ±0,000 — чистый пол жилых помещений
- низ потолка; серая полоса — стена без плитки
- (А) обозначение стены А–Г (как на развёртках)

Допущения и предложения на листе

Основа листа: размеры сняты с растрового плана заказчика без размеров: масштаб восстановлен по площадям помещений (≈ 11,8 мм на пиксель), контрольный обмер не выполнен (К-1); высота потолка 2700 мм принята: на плане заказчика её нет (К-2); толщины стен 300 / 120 мм приняты по плану заказчика, не замерены (К-1); разрешённая мощность 15 кВт принята по типовым ТУ для квартиры, ТУ заказчиком не переданы (К-4); подрайон климата не задан — принят не северный (жилые от 2,5 м) (К-9).
См. лист открытых вопросов (лист 6, записи К-1, К-2, К-4; лист 7, запись К-9).

1000 мм · печать 1:1

Изм.	Кол.уч	Лист	№ док.	Подп.	Дата
Разраб.		Кырлан А.С.			14.11.26
Пров.					
ГИП					
Н. контр.					
Утв.					

ГД-2026-007-АИ

Квартира 65 м²

Общая площадь 65,24* м² · * размеры со скана, не замерены (реестр — л. 6–8, К-1)

Дизайн-проект интерьера

Стадия	Лист	Листов
РП	55	117

Раскладка плитки. Ванная. Развёртки стен

М 1:25

Кырлан Александр Сергеевич

выпуск 14.11.2026 № 9cc0b98f36 · стр. 61 из 139

07

Полы и отделка

Кырлан Александр Сергеевич

выпуск 14.11.2026 № 9cc0b98f36 · стр. 62 из 139

План полов

Покрытия, направление укладки, отметки чистого пола, стыки · размеры в мм · отметки в м



Условные обозначения


- тип 1 — инженерная доска, линии — вдоль доски
- тип 2 — керамогранит 600×1200, сетка — формат плитки
- тип 3 — керамогранит 600×1200, сетка — формат плитки
- 1 — номер типа пола (экспликация полов)
- схема пола, без масштаба: плита — штриховка, стяжка — точки, звукоизоляция — зигзаг, гидроизоляция — утолщённая линия с заведением на стену
- направление укладки (длинная сторона доски)
- отметка чистого пола, м
- стык в проёме: решение не задано
- стык в проёме: без порога (б/п)
- стык в проёме: порог
- CT1 — марка стыка (ведомость стыков)
- стояк: К1 — канализация, В1 ХВС, Т3 — ГВС
- новое — возводится по проекту (синим)
- 1 — номер помещения, площадь м²

Отметки по высоте

±0,000	чистый пол пом. 1–5, 8, 9; отсчёт высот
−0,015	чистый пол пом. 6, 7, ниже на 15 мм
−0,064*	верх плиты — расчёт, не замер (задание на обмер)
сущ. пол	снимается до плиты; не замерен (задание на обмер)

Экспликация полов

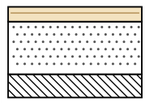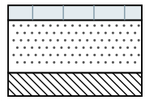Номер помещения	Тип пола	Схема пола	Данные элементов пола (наименование, толщина, основание), мм	Площадь, м²
1, 2, 3, 8, 9	1		Инженерная доска на клею — 14 Стяжка ЦПС М200 — 50 Плита перекрытия Всего 64 мм; ЧП ±0,000, верх плиты −0,064	49,90
4, 5	2		Керамогранит на клею С2 TE S1 — 14 Стяжка ЦПС М200 — 50 Плита перекрытия Всего 64 мм; ЧП ±0,000, верх плиты −0,064	9,66
6, 7	3		Керамогранит на клею С2 TE S1 — 14 Гидроизоляция обмазочная, 2 слоя, с заведением на стены 200 мм — 2 Стяжка ЦПС М200 — 33 Плита перекрытия Всего 49 мм; ЧП −0,015, верх плиты −0,064	5,68
			Итого	**65,24**

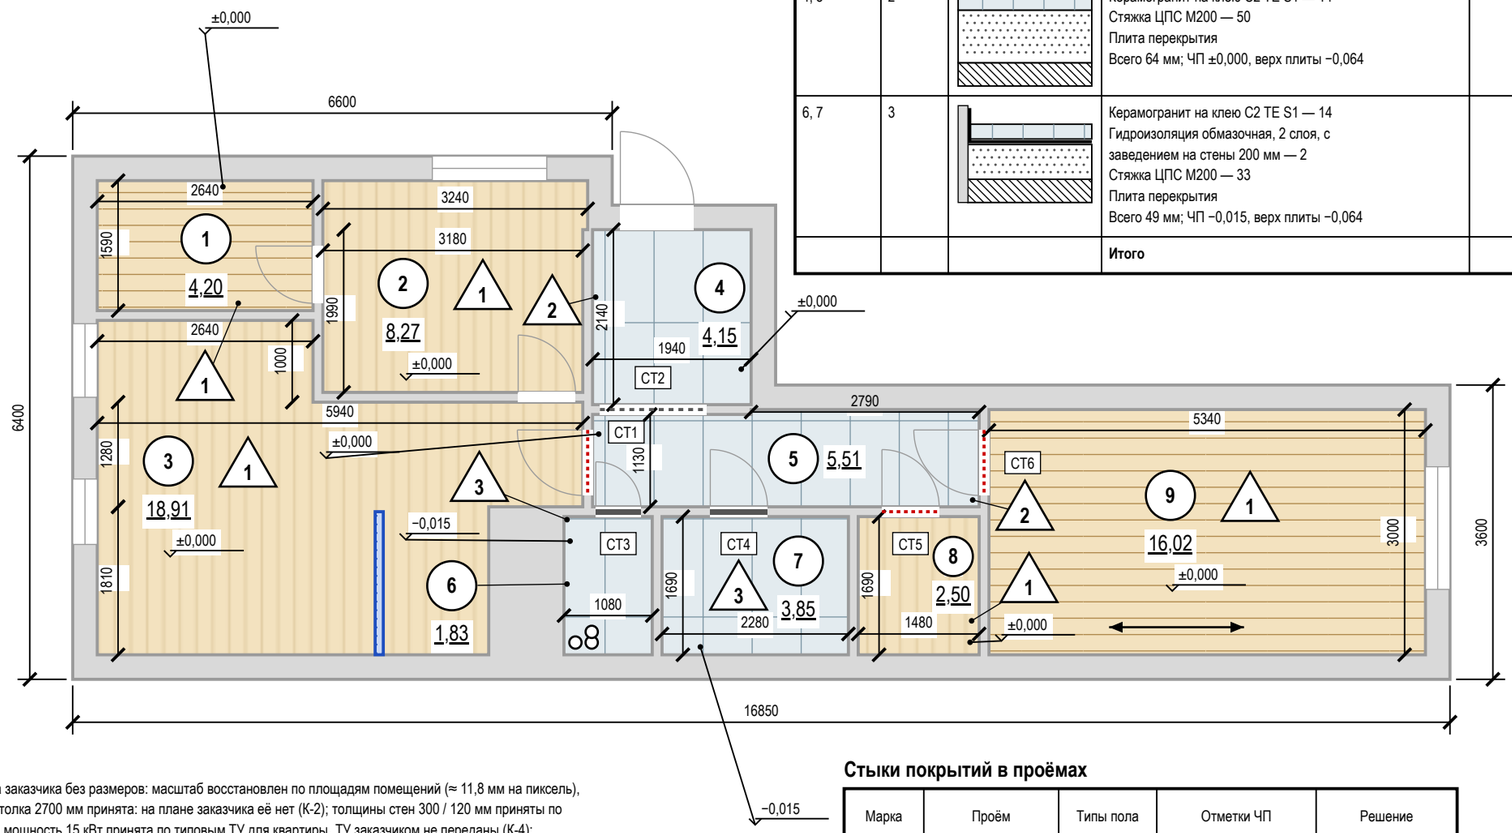

Допущения и предложения на листе

Основа листа: размеры сняты с растрового плана заказчика без размеров: масштаб восстановлен по площадям помещений (≈ 11,8 мм на пиксель), контрольный обмер не выполнен (К-1); высота потолка 2700 мм принята: на плане заказчика её нет (К-2); толщины стен 300 / 120 мм приняты по плану заказчика, не замерены (К-1); разрешённая мощность 15 кВт принята по типовым ТУ для квартиры, ТУ заказчиком не переданы (К-4); подрайон климата не задан — принят не северный (жилые от 2,5 м) (К-9).

Знак «**» — предложение проектировщика, заказчиком не утверждено (согласовать с заказчиком): пол пом. 1–3, 8, 9 — артикул выбран из каталога: Coswick 1167-1101 (инженерная доска, дуб натуральный, лак, 2100×127 мм); предложение исполнителя — выбор подтверждает автор; цены в каталоге нет, в смете «по КП».

См. лист открытых вопросов (лист 6, записи К-1, К-2, К-4; лист 7, запись К-9).

Стыки покрытий в проёмах

Марка	Проём	Типы пола	Отметки ЧП	Решение
CT1	3–5 (Д-2)	1 / 2	±0,000 / ±0,000	не задано
CT2	4–5	2 / 2	±0,000 / ±0,000	б/п
CT3	5–6 (Д-5)	2 / 3	±0,000 / −0,015	порог h=15 мм
CT4	5–7 (Д-4)	2 / 3	±0,000 / −0,015	порог h=15 мм
CT5	5–8 (Д-3)	2 / 1	±0,000 / ±0,000	не задано
CT6	5–9 (Д-2)	2 / 1	±0,000 / ±0,000	не задано

Примечания

1. За отметку ±0,000 принят чистый пол, не существующий (блок отметок). Площади — по чистым размерам помещений, м²; размеры — в мм.
2. Стык разнотипных покрытий — по оси дверного полотна (под полотном в закрытом положении); решение стыка — по ведомости стыков.
3. Размеры помещений в свету (ширина × длина, мм), не поместившиеся на плане: пом. 2 — 3240 × 600, 3180 × 1990; пом. 3 — 2640 × 1000, 5940 × 1280, 4790 × 1810; пом. 5 — 2790 × 60, 4730 × 1130; пом. 6 — 1080 × 1690.
4. Пол санузлов ниже смежных помещений на 15 мм за счёт меньшей толщины стяжки (верх плиты общий — по экспликации полов); гидроизоляция по стяжке с заведением на стены не менее 200 мм (СП 29.13330.2011, п. 7.2), до облицовки — тест проливом и акт скрытых работ.
5. Выпуски канализации с уклоном и трассы водоснабжения — в слое засыпки под стяжкой (по экспликации полов); отметки, уклоны и прочистки — по листу разводки ВК 40.
6. Звукоизоляционный слой под стяжкой проектом не предусмотрен (стяжка по плите): приведённый уровень ударного шума перекрытия с полом Lnw не более 60 дБ (СП 51.13330.2011, табл. 2) подтвердить по данным дома; при превышении — плавающая стяжка по звукоизоляции с демпферной лентой по контуру и у стояков, пирог пересчитать.
7. Штучные покрытия (инженерная доска): направление — по стрелке; влажность основания по СМ не более 2,0 % (по ТУ изготовителя).
8. Ровность основания — просвет под 2-метровой рейкой не более 2 мм: пом. 1, 2, 3, 8, 9 (инженерная доска), пом. 4, 5, 6, 7 (керамогранит); проверить до укладки покрытия (СП 71.13330.2017, табл. 8.5).
9. Сетка на плитке — условная, в размер формата; точка старта и раскладка — по листу раскладки плитки.
10. Узор покрытия (заливка-код типа пола) прерывается под надписями — площадями помещений и отметками чистого пола.
11. Пироги полов — по экспликации полов: слои сверху вниз, толщины в мм; гидроизоляция мокрых зон — в пироге и в ведомости отделки; схема пола — без масштаба.

1000 мм · печать 1:1

Изм.	Кол.уч	Лист	№ док.	Подп.	Дата
Разраб.		Кырлан А.С.			14.11.26
Пров.					
ГИП					
Н. контр.					
Утв.					

ГД-2026-007-АИ

Квартира 65 м²

Общая площадь 65,24* м² · * размеры со скана, не замерены (реестр — л. 6–8, К-1)

Дизайн-проект интерьера

Стадия	Лист	Листов
РП	56	117

План полов

М 1:75

Кырлан Александр Сергеевич

Ведомость отделки помещений

Потолки, стены, низ стен, полы · площади в м², длины в м · отметки в м

Ведомость отделки помещений (форма 1 прил. А ГОСТ 21.501-2018)

№	Наименование помещения	Потолок			Стены и перегородки			Низ стен (плинтус)			Пол		Примечание
		Вид отделки	Код цвета	S, м²	Вид отделки	Код цвета	S, м²	Вид отделки	Код цвета	L, м	Вид отделки	S, м²	
1	Гардеробная 4,20 м²	Существующий потолок, отм. +2,700; окраска, Tikkurila Anti-Reflex 2, глубокоматовая, 2 слоя, подготовка Q3	Tikkurila V503	4,20	Окраска, Tikkurila Harmony, матовая, 2 слоя, подготовка Q3	Tikkurila V503	21,37	Плинтус МДФ h=69 мм, SX165	Tikkurila V503	7,8	Инженерная доска, 1167-1101, 2100×127 мм, на клею; тип 1, отм. ЧП ±0,000	4,20	Н стен 2700 (до потолка); плинтус в цвет: стены
2	Спальня 8,27 м²	ГКЛ по каркасу П113, отм. +2,600; окраска, Tikkurila, глубокоматовая	NCS S 0300-N	8,27	Окраска, Tikkurila, глубокоматовая, подготовка Q3	NCS S 1502-Y50R	25,14	Плинтус МДФ h=69 мм, SX165	NCS S 0300-N	10,3	Инженерная доска, 1167-1101, 2100×127 мм, на клею; тип 1, отм. ЧП ±0,000	8,27	Н стен 2600 (до потолка)
3	Кухня-гостиная 18,91 м²	ГКЛ по каркасу П113, отм. +2,600; окраска, Tikkurila, глубокоматовая	NCS S 0300-N	18,91	Окраска, Tikkurila, полуматовая, подготовка Q3	NCS S 1002-Y50R	46,29	Плинтус МДФ h=69 мм, SX165	NCS S 0300-N	18,6	Инженерная доска, 1167-1101, 2100×127 мм, на клею; тип 1, отм. ЧП ±0,000	18,91	Н стен 2600 (до потолка)
4	Прихожая 4,15 м²	ГКЛ по каркасу П113, отм. +2,600; окраска, Tikkurila, глубокоматовая	NCS S 0300-N	4,15	Окраска, Tikkurila, полуматовая, подготовка Q3	NCS S 1502-Y50R	16,60	Плинтус МДФ h=69 мм, SX165	NCS S 0300-N	6,0	Керамогранит, SG501600R, 600×1200 мм; тип 2, отм. ЧП ±0,000	4,15	Н стен 2600 (до потолка)
5	Коридор 5,51 м²	ГКЛ по каркасу П113, отм. +2,600; окраска, Tikkurila, глубокоматовая	NCS S 0300-N	5,51	Окраска, Tikkurila, полуматовая, подготовка Q3	NCS S 1502-Y50R	20,60	Плинтус МДФ h=69 мм, SX165	NCS S 0300-N	7,0	Керамогранит, SG501600R, 600×1200 мм; тип 2, отм. ЧП ±0,000	5,51	Н стен 2600 (до потолка)
6	Санузел 1,83 м²	ГКЛВ по каркасу П113, отм. +2,600; окраска, Tikkurila, глубокоматовая	NCS S 0300-N	1,83	Облицовка плиткой, 610010001195, 600×1200 мм, клей С2	Italon 610010001195	13,33	нет (облицовка от пола)			Керамогранит, SG501600R, 600×1200 мм; тип 3, отм. ЧП −0,015	1,83	Н стен 2615 (до потолка); гидроизоляция обмазочная, 2 слоя, с заведением на стены 200 мм (по пирогу пола); тест проливом и акт скрытых работ
7	Ванная 3,85 м²	ГКЛВ по каркасу П113, отм. +2,600; окраска, Tikkurila, глубокоматовая	NCS S 0300-N	3,85	Облицовка плиткой, 610010001195, 600×1200 мм, клей С2	Italon 610010001195	19,29	нет (облицовка от пола)			Керамогранит, SG501600R, 600×1200 мм; тип 3, отм. ЧП −0,015	3,85	Н стен 2615 (до потолка); тёплый пол; гидроизоляция обмазочная, 2 слоя, с заведением на стены 200 мм; над ванной — до 2000 и 300 мм за борт (по пирогу пола); тест проливом и акт скрытых работ
8	Кладовая 2,50 м²	Существующий потолок, отм. +2,700; окраска, Tikkurila, глубокоматовая	NCS S 0300-N	2,50	Окраска, Tikkurila, матовая, подготовка Q3	NCS S 0502-Y	15,65	Плинтус МДФ h=69 мм, SX165	NCS S 0300-N	5,6	Инженерная доска, 1167-1101, 2100×127 мм, на клею; тип 1, отм. ЧП ±0,000	2,50	Н стен 2700 (до потолка)
9	Детская 16,02 м²	ГКЛ по каркасу П113, отм. +2,500; +2,600; окраска, Tikkurila Anti-Reflex 2, глубокоматовая, 2 слоя, подготовка Q3	Tikkurila V503	16,02	Окраска, Farrow & Ball Modern Emulsion, матовая, 2 слоя, подготовка Q3 Акцент — стена А: окраска, Farrow & Ball Modern Emulsion, матовая, 2 слоя, подготовка Q3	Farrow & Ball No. 241 Farrow & Ball No. 30	24,27 13,35	Плинтус МДФ h=69 мм, SX165	Farrow & Ball No. 241	15,9	Инженерная доска, 1167-1101, 2100×127 мм, на клею; тип 1, отм. ЧП ±0,000	16,02	Н стен 2500 (до потолка); плинтус в цвет: стены
	Итого			**65,24**			**215,88**			**71,1**		**65,24**	

Допущения и предложения на листе

Основа листа: размеры сняты с растрового плана заказчика без размеров: масштаб восстановлен по площадям помещений (≈ 11,8 мм на пиксель), контрольный обмер не выполнен (К-1); высота потолка 2700 мм принята: на плане заказчика её нет (К-2); толщины стен 300 / 120 мм приняты по плану заказчика, не замерены (К-1); разрешённая мощность 15 кВт принята по типовым ТУ для квартиры, ТУ заказчиком не переданы (К-4); подрайон климата не задан — принят не северный (жилые от 2,5 м) (К-9).

Знак «**» — предложение проектировщика, заказчиком не утверждено (согласовать с заказчиком): пол пом. 1–3, 8, 9 — артикул выбран из каталога: Coswick 1167-1101 (инженерная доска, дуб натуральный, лак, 2100×127 мм); предложение исполнителя — выбор подтверждает автор; цены в каталоге нет, в смете «по КП».

См. лист открытых вопросов (лист 6, записи К-1, К-2, К-4; лист 7, запись К-9).

Примечания

1. Площади поверхностей — по чистым граням стен до отделки: стены = периметр × высоту от чистого пола помещения до низа потолка минус проёмы (облицовка плиткой — до верха облицовки); плинтус = периметр минус дверные проёмы; пол и потолок — по площади помещения. Количество плиток по раскладке. Площади помещений — с учётом всех частей помещения; откосы в площадь стен не входят.
2. Акцентные стены — отдельными строками, их площадь вычтена из основной отделки стен помещения.
3. Плинтус — длина по периметру за вычетом дверных проёмов; примыкания к наличникам и встроенной мебели — по развёрткам.
4. Формат плитки — Ш×В×Т (ширина × высота в положении укладки × толщина), мм; на полу — вдоль стен А/В × вдоль стен Б/Г.
5. Коды цвета — по веерам производителей; колеровка каждой краски одной партией, проверка выкраса при свете D65 и при лампах проекта.
6. Уровни подготовки Q1–Q4 — система Knauf, не норма ГОСТ/СП; допуски поверхностей — по СП 71.13330.2017 (действующая редакция).
7. «аналог:» — изделие задано характеристиками, марку и артикул согласовать с заказчиком до закупки.
8. Сводка площадей по материалам, м²: потолок — Tikkurila V503 Anti-Reflex 2 — 20,22; потолок — NCS S 0300-N — 45,02; стены — Tikkurila V503 Harmony — 21,37; стены — NCS S 1502-Y50R — 62,33; стены — NCS S 1002-Y50R — 46,29; стены — облицовка плиткой 600×1200 мм, Italon 610010001195 — 32,63; стены — NCS S 0502-Y — 15,65; стены — Farrow & Ball No. 241 Modern Emulsion — 24,27; стены — Farrow & Ball No. 30 Modern Emulsion 13,35.

Изм.	Кол.уч	Лист	№ док.	Подп.	Дата
Разраб.		Кырлан А.С.			14.11.26
Пров.					
ГИП					
Н. контр.					
Утв.					

ГД-2026-007-АИ

Квартира 65 м²

Общая площадь 65,24* м² · * размеры со скана, не замерены (реестр — л. 6–8, К-1)

Дизайн-проект интерьера

Стадия	Лист	Листов
РП	57	117

Ведомость отделки помещений

М б/м

Кырлан Александр Сергеевич

выпуск 14.11.2026 № 9cc0b98f36 · стр. 64 из 139

Колерная карта

Цвета и материалы по помещениям · палитра проекта · выкрасы на согласование

ПРЕДВАРИТЕЛЬНО · не для производства работ · открыто пунктов: 14 (реестр — л. 6–8)

Колерная карта по помещениям

Помещение	Поверхность	Образец	Поз.	Система и код цвета	Производитель, линейка / материал, артикул	Блеск	Класс истирания	LRV	Площадь
1. Гардеробная 4,2 м²	стены		**К1**	Tikkurila V503	Tikkurila · Harmony	матовая	1	86	21,4 м²
	потолок		**К2**	Tikkurila V503	Tikkurila · Anti-Reflex 2	глубокомат.	2	86	4,2 м²
	пол		**КМ1**	по образцу	Coswick · Классическая · арт. 1167-1101				4,2 м²
	плинтус		**К3**	Tikkurila V503	Orac Decor · Contour (Luxxus)			86	7,8 м
2. Спальня 8,27 м²	стены		**К4**	NCS S 1502-Y50R	Tikkurila	глубокомат.	2	72	25,1 м²
	потолок		**К5**	NCS S 0300-N	Tikkurila	глубокомат.	2	92	8,3 м²
	пол		**КМ1**	по образцу	Coswick · Классическая · арт. 1167-1101				8,3 м²
	плинтус		**К6**	NCS S 0300-N	Orac Decor · Contour (Luxxus)	полуматов.		92	10,3 м
3. Кухня-гостиная 18,91 м²	стены		**К7**	NCS S 1002-Y50R	Tikkurila	полуматов.	1	82	46,3 м²
	потолок		**К8**	NCS S 0300-N	Tikkurila	глубокомат.	1	92	18,9 м²
	пол		**КМ1**	по образцу	Coswick · Классическая · арт. 1167-1101				18,9 м²
	плинтус		**К6**	NCS S 0300-N	Orac Decor · Contour (Luxxus)	полуматов.		92	18,6 м
4. Прихожая 4,15 м²	стены		**К9**	NCS S 1502-Y50R	Tikkurila	полуматов.	1	72	16,6 м²
	потолок		**К8**	NCS S 0300-N	Tikkurila	глубокомат.	1	92	4,2 м²
	пол		**КМ2**	Королевская дорога	Kerama Marazzi · арт. SG501600R				4,2 м²
	плинтус		**К6**	NCS S 0300-N	Orac Decor · Contour (Luxxus)	полуматов.		92	6,0 м
5. Коридор 5,51 м²	стены		**К9**	NCS S 1502-Y50R	Tikkurila	полуматов.	1	72	20,6 м²
	потолок		**К8**	NCS S 0300-N	Tikkurila	глубокомат.	1	92	5,5 м²
	пол		**КМ2**	Королевская дорога	Kerama Marazzi · арт. SG501600R				5,5 м²
	плинтус		**К6**	NCS S 0300-N	Orac Decor · Contour (Luxxus)	полуматов.		92	7,0 м
6. Санузел 1,83 м²	стены		**КМ3**	Charme Extra	Italon · арт. 610010001195				13,3 м²
	потолок		**К8**	NCS S 0300-N	Tikkurila	глубокомат.	1	92	1,8 м²
	пол		**КМ2**	Королевская дорога	Kerama Marazzi · арт. SG501600R				1,8 м²
7. Ванная 3,85 м²	стены		**КМ3**	Charme Extra	Italon · арт. 610010001195				19,3 м²
	потолок		**К8**	NCS S 0300-N	Tikkurila	глубокомат.	1	92	3,9 м²
	пол		**КМ2**	Королевская дорога	Kerama Marazzi · арт. SG501600R				3,9 м²
8. Кладовая 2,5 м²	стены		**К10**	NCS S 0502-Y	Tikkurila	матовая	2	86	15,6 м²
	потолок		**К5**	NCS S 0300-N	Tikkurila	глубокомат.	2	92	2,5 м²
	пол		**КМ1**	по образцу	Coswick · Классическая · арт. 1167-1101				2,5 м²
	плинтус		**К6**	NCS S 0300-N	Orac Decor · Contour (Luxxus)	полуматов.		92	5,6 м
9. Детская 16,02 м²	стены		**К11**	Farrow & Ball No. 241	Farrow & Ball · Modern Emulsion	матовая	1	67	24,3 м²
	акцент А		**К12**	Farrow & Ball No. 30	Farrow & Ball · Modern Emulsion	матовая	1	7	13,3 м²
	потолок		**К2**	Tikkurila V503	Tikkurila · Anti-Reflex 2	глубокомат.	2	86	16,0 м²
	пол		**КМ1**	по образцу	Coswick · Классическая · арт. 1167-1101				16,0 м²
	плинтус		**К13**	Farrow & Ball No. 241	Orac Decor · Contour (Luxxus)			67	15,9 м

Схема палитры проекта

Стиль: Скандинавский · схема: нейтральная

основной	основной	основной	основной	второстепенный	второстепенный	акцентный
NCS S 1502-Y50R	**NCS S 1002-Y50R**	**NCS S 0300-N**	**Tikkurila V503**	**Farrow & Ball No. 241**	**NCS S 0502-Y**	**Farrow & Ball No. 30**
тёплый светло-серый LRV 72 стены 2,4,5	тёплый светлый грейж LRV 82 стены 3	белый LRV 92 потолок 2,3,4,5,6,7,8; плинтус 2,3,4,5,8	Winter LRV 86 стены 1; потолок 1,9; плинтус 1; текстиль/декор 9	Skimming Stone LRV 67 стены 9; плинтус 9; текстиль/декор 4,7	белый сёдзи/сиккуй — известь, васи LRV 86 стены 8	Hague Blue LRV 7 акцент 9; текстиль/декор 9

План 60/30/10

60%	30%	10%

Окраска, факт — по площади стен, акцентов, потолков

79%	16%	

окрашено всего 248,5 м²; второстепенный тон несут мебель и текстиль

Текстиль и декор в цветах вне палитры проекта

- Tikkurila G503 Calla — пом. 2 (Т6**, Т15**), 3 (Т1**, Т2**, Т3**), 7 (Т19**)
- NCS S 2002-Y серый камень, тёплый — пом. 2 (Т13**)
- Farrow & Ball No. 231 Setting Plaster — пом. 2 (Т14**)
- Farrow & Ball No. 299 De Nimes — пом. 2 (Т16**), 3 (Т4**), 7 (Т18**)
- NCS S 3020-Y80R приглушённая терракота/пудра — пом. 3 (Т5**)
- Tikkurila H487 Pumice — пом. 9 (Т7)
- Tikkurila V484 Driftwood — пом. 9 (Т9)
- Farrow & Ball No. 229 Elephant's Breath — пом. 9 (Т10)
- Farrow & Ball No. 47 Green Smoke — пом. 9 (Т11)

Условные обозначения

- **К1** Tikkurila V503 · Winter · Harmony · матовая · кл. 1
- **К2** Tikkurila V503 · Winter · Anti-Reflex 2 · глубокомат. · кл. 2
- **К3** Tikkurila V503 · Winter · Contour (Luxxus)
- **К4** NCS S 1502-Y50R · Tikkurila · глубокомат. · кл. 2
- **К5** NCS S 0300-N · Tikkurila · глубокомат. · кл. 2
- **К6** NCS S 0300-N · Orac Decor Contour (Luxxus) · полуматов.
- **К7** NCS S 1002-Y50R · Tikkurila · полуматов. · кл. 1
- **К8** NCS S 0300-N · Tikkurila · глубокомат. · кл. 1
- **К9** NCS S 1502-Y50R · Tikkurila · полуматов. · кл. 1
- **К10** NCS S 0502-Y · Tikkurila · матовая · кл. 2
- **К11** Farrow & Ball No. 241 · Skimming Stone · Modern Emulsion · матовая · кл. 1
- **К12** Farrow & Ball No. 30 · Hague Blue · Modern Emulsion · матовая · кл. 1
- **К13** Farrow & Ball No. 241 · Skimming Stone · Contour (Luxxus)
- **КМ1** инженерная доска · 1167-1101
- **КМ2** керамогранит · SG501600R
- **КМ3** плитка · 610010001195

дерево (доска, паркет, ламинат) — рисунок досок

керамогранит, плитка, камень — сетка швов по формату

плашка не залита — цвет только по коду и вееру бренда

К — краска, КМ — отделочный материал (тон КМ — по описанию, эталон — образец материала); кл. — класс истирания (1 — самый стойкий к мытью); LRV — светлота цвета: 0 — чёрный, 100 — белый

Перечень выкрасов на согласование

№	Код	Бренд / веер	Пом. / стена	Подложка	Формат	Статус

… ещё 7 выкрасов — в ведомости отделки

Примечания

1. Цвет на листе и на экране — ориентир. До покраски — выкрас на объекте: не меньше А3 (или лист ГКЛ), на грунте под эту краску, не на белой шпаклёвке, в 2 слоя; на обороте — код, бренд, веер, дата. Смотреть днём и вечером, рядом с образцами пола и плитки; к основному цвету стен — ещё 2 соседних оттенка. Красить только в цвет утверждённого выкраса.
2. Краску заказывать по коду из графы «Система и код цвета» у бренда этого кода, не «аналогом» другого; весь объём одного кода — одной партией, колеруемую краску — за один проход машины.
3. Площади — те же, что в ведомости отделки (лист 57); сколько краски заказать — в спецификации отделочных материалов (лист 59).

Допущения и предложения на листе

Основа листа: размеры сняты с растрового плана заказчика без размеров: масштаб восстановлен по площадям помещений (≈ 11,8 мм на пиксель), контрольный обмер не выполнен (К-1); высота потолка 2700 мм принята: на плане заказчика её нет (К-2); толщины стен 300 / 120 мм приняты по плану заказчика, не замерены (К-1); разрешённая мощность 15 кВт принята по типовым ТУ для квартиры, ТУ заказчиком не переданы (К-4); подрайон климата не задан — принят не северный (жилые от 2,5 м) (К-9).

Знак «**» — предложение проектировщика, заказчиком не утверждено (согласовать с заказчиком): пол пом. 1–3, 8, 9 — артикул выбран из каталога: Coswick 1167-1101 (инженерная доска, дуб натуральный, лак, 2100×127 мм); предложение исполнителя — выбор подтверждает автор; цены в каталоге нет, в смете «по КП»; ИЗ-4: Т6, Т13, Т14, Т15, Т16, Т1, Т2, Т3, Т4, Т5; ИЗ-5: Т18, Т19.

См. лист открытых вопросов (лист 6, записи К-1, К-2, К-4; лист 7, запись К-9; лист 8, записи ИЗ-4, ИЗ-5).

Изм.	Кол.уч	Лист	№ док.	Подп.	Дата
Разраб.		Кырлан А.С.			14.11.26
Пров.					
ГИП					
Н. контр.					
Утв.					

ГД-2026-007-АИ

Квартира 65 м²

Общая площадь 65,24* м² · * размеры со скана, не замерены (реестр — л. 6–8, К-1)

Дизайн-проект интерьера

Стадия	Лист	Листов
РП	58	117

Колерная карта

М б/м

Кырлан Александр Сергеевич

Спецификация отделочных материалов

ПРЕДВАРИТЕЛЬНО · не для производства работ · открыто пунктов: 14 (реестр — л. 6–8)

Форма 1 по ГОСТ 21.110-2013 · количества — из геометрии проекта, с запасом · часть 1 из 2

Поз.	Наименование и техническая характеристика	Тип, марка, обозначение документа	Код продукции	Поставщик	Ед. изм.	Кол.	Масса 1 ед., кг	Примечание
	Лакокрасочные материалы							
1	Краска интерьерная водно-дисперсионная акриловая для стен, матовая, класс мокрого истирания 1 по EN 13300, база A; цвет по вееру Tikkurila V503 «Winter», колеровка машинная	Tikkurila Harmony		Tikkurila	л	6,3		поз. К1 колерной карты; пом. 1; S = 21,4 м² × 2 сл. × 0,12 л/м² = 5,1 л, +10 % и 0,5 л на подкраску → ≥ 6,1 л; тара 2 × 2,7 л + 1 × 0,9 л
2	Краска интерьерная водно-дисперсионная акриловая для потолков, глубокоматовая, класс мокрого истирания 2 по EN 13300, база A; цвет по вееру Tikkurila V503 «Winter», колеровка машинная	Tikkurila Anti-Reflex 2		Tikkurila	л	6,3		поз. К2 колерной карты; пом. 1, 9; S = 20,2 м² × 2 сл. × 0,12 л/м² = 4,9 л, +10 % и 0,5 л на подкраску → ≥ 5,8 л; тара 2 × 2,7 л + 1 × 0,9 л
3	Краска интерьерная водно-дисперсионная акриловая для стен, глубокоматовая, класс мокрого истирания 2 по EN 13300, база A; цвет NCS S 1502-Y50R, колеровка машинная	Tikkurila		Tikkurila	л	7,2		поз. К4 колерной карты; пом. 2; S = 25,1 м² × 2 сл. × 0,12 л/м² = 6,0 л, +10 % и 0,5 л на подкраску → ≥ 7,1 л; тара 2 × 2,7 л + 2 × 0,9 л
4	Краска интерьерная водно-дисперсионная для потолков, глубокоматовая, класс мокрого истирания 2 по EN 13300, база A; цвет NCS S 0300-N, колеровка машинная	Tikkurila		Tikkurila	л	3,6		поз. К5 колерной карты; пом. 2, 8; S = 10,8 м² × 2 сл. × 0,12 л/м² = 2,6 л, +10 % и 0,5 л на подкраску → ≥ 3,3 л; тара 1 × 2,7 л + 1 × 0,9 л
5	Краска интерьерная водно-дисперсионная акриловая для стен, полуматовая, класс мокрого истирания 1 по EN 13300, база A; цвет NCS S 1002-Y50R, колеровка машинная	Tikkurila		Tikkurila	л	13,5		поз. К7 колерной карты; пом. 3; S = 46,3 м² × 2 сл. × 0,12 л/м² = 11,1 л, +10 % и 0,5 л на подкраску → ≥ 12,7 л; тара 1 × 9 л + 1 × 2,7 л + 2 × 0,9 л
6	Краска интерьерная водно-дисперсионная для потолков, глубокоматовая, класс мокрого истирания 1 по EN 13300, база A; цвет NCS S 0300-N, колеровка машинная	Tikkurila		Tikkurila	л	9,9		поз. К8 колерной карты; пом. 3, 4, 5, 6, 7; S = 34,3 м² × 2 сл. × 0,12 л/м² = 8,2 л, +10 % и 0,5 л на подкраску → ≥ 9,5 л; тара 1 × 9 л + 1 × 0,9 л
7	Краска интерьерная водно-дисперсионная акриловая для стен, полуматовая, класс мокрого истирания 1 по EN 13300, база A; цвет NCS S 1502-Y50R, колеровка машинная	Tikkurila		Tikkurila	л	10,8		поз. К9 колерной карты; пом. 4, 5; S = 37,2 м² × 2 сл. × 0,12 л/м² = 8,9 л, +10 % и 0,5 л на подкраску → ≥ 10,3 л; тара 1 × 9 л + 2 × 0,9 л
8	Краска интерьерная водно-дисперсионная акриловая для стен, матовая, класс мокрого истирания 2 по EN 13300, база A; цвет NCS S 0502-Y, колеровка машинная	Tikkurila		Tikkurila	л	5,4		поз. К10 колерной карты; пом. 8; S = 15,6 м² × 2 сл. × 0,12 л/м² = 3,8 л, +10 % и 0,5 л на подкраску → ≥ 4,6 л; тара 2 × 2,7 л
9	Краска интерьерная водно-дисперсионная акриловая для стен, матовая, класс мокрого истирания 1 по EN 13300, база A; цвет по вееру Farrow & Ball No. 241 «Skimming Stone», колеровка машинная	Farrow & Ball Modern Emulsion		Farrow & Ball	л	7,5		поз. К11 колерной карты; пом. 9; S = 24,3 м² × 2 сл. × 0,12 л/м² = 5,8 л, +10 % и 0,5 л на подкраску → ≥ 6,9 л; тара 1 × 5 л + 1 × 2,5 л
10	Краска интерьерная водно-дисперсионная акриловая для акцентных стен, матовая, класс мокрого истирания 1 по EN 13300, база C; цвет по вееру Farrow & Ball No. 30 «Hague Blue», колеровка машинная	Farrow & Ball Modern Emulsion		Farrow & Ball	л	5		поз. К12 колерной карты; пом. 9; S = 13,3 м² × 2 сл. × 0,12 л/м² = 3,2 л, +10 % и 0,5 л на подкраску → ≥ 4,0 л; тара 1 × 5 л
11	Краска для МДФ и дерева в цвет Tikkurila V503 «Winter» — окраска плинтуса; блеск не ниже блеска стен	марка не задана			л	0,5		поз. К3; пом. 1; L = 7,8 м, S = 0,7 м² × 2 сл. × 0,12 л/м² + 10 %; продукт подобрать в веере Tikkurila
12	Акрил, полуматовая в цвет NCS S 0300-N — окраска плинтуса	аналог по характеристикам			л	1,1		поз. К6; пом. 2, 3, 4, 5, 8; L = 47,4 м, S = 4,0 м² × 2 сл. × 0,12 л/м² + 10 %; продукт подобрать в веере NCS
13	Краска для МДФ и дерева в цвет Farrow & Ball No. 241 «Skimming Stone» — окраска плинтуса; блеск не ниже блеска стен	марка не задана			л	0,5		поз. К13; пом. 9; L = 15,9 м, S = 1,3 м² × 2 сл. × 0,12 л/м² + 10 %; продукт подобрать в веере Farrow & Ball
14	Грунтовка акриловая под окраску стен и потолков — из системы производителя краски	по системе краски			м²	249		площадь окраски стен, акцентов и потолков; 1 слой перед окраской; расход — по ТУ грунтовки

Допущения и предложения на листе

Основа листа: размеры сняты с растрового плана заказчика без размеров: масштаб восстановлен по площадям помещений (≈ 11,8 мм на пиксель), контрольный обмер не выполнен (К-1); высота потолка 2700 мм принята: на плане заказчика её нет (К-2); толщины стен 300 / 120 мм приняты по плану заказчика, не замерены (К-1); разрешённая мощность 15 кВт принята по типовым ТУ для квартиры, ТУ заказчиком не переданы (К-4); подрайон климата не задан — принят не северный (жилые от 2,5 м) (К-9).

Знак «**» — предложение проектировщика, заказчиком не утверждено (согласовать с заказчиком): пол пом. 1–3, 8, 9 — артикул выбран из каталога: Coswick 1167-1101 (инженерная доска, дуб натуральный, лак, 2100×127 мм); предложение исполнителя — выбор подтверждает автор; цены в каталоге нет, в смете «по КП».

См. лист открытых вопросов (лист 6, записи К-1, К-2, К-4; лист 7, запись К-9).

Изм.	Кол.уч	Лист	№ док.	Подп.	Дата
Разраб.		Кырлан А.С.			14.11.26
Пров.					
ГИП					
Н. контр.					
Утв.					

ГД-2026-007-АИ

Квартира 65 м²

Общая площадь 65,24* м² · * размеры со скана, не замерены (реестр — л. 6–8, К-1)

Дизайн-проект интерьера	Стадия	Лист	Листов
	РП	59	117
Спецификация отделочных материалов М б/м	**Кырлан Александр Сергеевич**		

выпуск 14.11.2026 № 9cc0b98f36 · стр. 66 из 139

Спецификация отделочных материалов

ПРЕДВАРИТЕЛЬНО · не для производства работ · открыто пунктов: 14 (реестр — л. 6–8)

Форма 1 по ГОСТ 21.110-2013 · количества — из геометрии проекта, с запасом · часть 2 из 2

Поз.	Наименование и техническая характеристика	Тип, марка, обозначение документа	Код продукции	Поставщик	Ед. изм.	Кол.	Масса 1 ед., кг	Примечание
	Плитка и керамогранит							
15	SG501600R, 600×1200 мм, противоскольжение R10	SG501600R		Kerama Marazzi	м²	23,04		шов 2 мм; Санузел, пол; Ванная, пол; Прихожая, пол; Коридор, пол; по раскладке 28 шт (S = 15,34 м²), с запасом 32 шт
16	610010001195, 1200×600 мм	610010001195		Italon	м²	56,16		шов 2 мм; Санузел, стены А–Г; Ванная, стены А–Г; по раскладке 70 шт (S = 32,62 м²), с запасом 78 шт
	Напольные покрытия							
17	1167-1101, рабочий слой 4 мм, эмиссия E1, укладка на клей	1167-1101		Coswick	м²	21,8		пом. 1, 9; S = 20,35 м² (пол + половина стены в дверных проёмах, как в смете) + 7 %; к заказу — кратно упаковке
18	1167-1101, класс 33, рабочий слой 4 мм, эмиссия E1, укладка на клей	1167-1101		Coswick	м²	32		пом. 2, 3, 8; S = 29,86 м² (пол + половина стены в дверных проёмах, как в смете) + 7 %; к заказу — кратно упаковке
19	Клей для паркета и инженерной доски, эластичный (СМП / полиуретановый)	по рекомендации производителя доски			м²	51		площадь приклейки; расход и шпатель — по ТУ клея
	Погонажные изделия							
20	SX165, h = 69 мм, крепление к стене, окраска в цвет Tikkurila V503	SX165		Orac Decor	м	9		пом. 1; L = 7,8 м (периметр без дверных проёмов) + 10 % на подрезку; в штуках — по длине планки
21	SX165, h = 69 мм, крепление к стене, окраска в цвет NCS S 0300-N	SX165		Orac Decor	м	53		пом. 2, 3, 4, 5, 8; L = 47,4 м (периметр без дверных проёмов) + 10 % на подрезку; в штуках — по длине планки
22	SX165, h = 69 мм, крепление к стене, окраска в цвет Farrow & Ball No. 241	SX165		Orac Decor	м	18		пом. 9; L = 15,9 м (периметр без дверных проёмов) + 10 % на подрезку; в штуках — по длине планки
	Смеси и материалы для облицовки							
23	Затирка для швов плитки	аналог по характеристикам			кг	3,7		по раскладке (a+b)/(a·b) × шов × t × 1,6 + 10 %
24	Клей плиточный C2 S1 по EN 12004, слой 5 мм	аналог по характеристикам			кг	36		2 меш. по 25 кг; 1,5 кг/м² на 1 мм слоя + 10 %
25	Клей плиточный C2 по EN 12004, слой 5 мм	аналог по характеристикам			кг	271		11 меш. по 25 кг; 1,5 кг/м² на 1 мм слоя + 10 %
26	Гидроизоляция обмазочная мокрых зон: пол, стены по периметру, зоны замачивания; 2 слоя с армирующей лентой в углах	аналог по характеристикам			м²	8,9		площадь по листу раскладки плитки + 10 %; расход смеси — по ТУ
27	Лента демпферная по периметру пола из плитки	аналог по характеристикам			м	27		периметр без дверных проёмов + 10 %

Примечания

1. Количества — из геометрии проекта: площади поверхностей по чистым граням стен до отделки (те же, что в ведомости отделки и колерной карте), плитка, клей и затирка — по раскладке плиточника; в графе «Кол.» — к заказу, с запасом.
2. Краска: расход 0,12 л/м² на слой в 2 слоя, если по ТУ не задан иной; запас 10 % и 0,5 л на подкраску каждого кода. Один код — одна партия, колеровка машинная в колеровочном центре бренда; в заказ — только после утверждения выкраса (колерная карта). Фасовка — по каталогу бренда на дату выпуска; к заказу — не меньше расчётного объёма.
3. «Аналог по характеристикам» — допускается изделие другого производителя с характеристиками не ниже указанных, по согласованию с автором проекта.
4. Графы «Код продукции» и «Масса 1 ед.» не заполнены: коды по классификатору продукции не присвоены, масса единицы до 25 кг (ГОСТ 21.110-2013).
5. Грунтовка и клей для доски указаны площадью обработки; объём — по ТУ выбранного продукта.

Допущения и предложения на листе

Основа листа: размеры сняты с растрового плана заказчика без размеров: масштаб восстановлен по площадям помещений (≈ 11,8 мм на пиксель), контрольный обмер не выполнен (К-1); высота потолка 2700 мм принята: на плане заказчика её нет (К-2); толщины стен 300 / 120 мм приняты по плану заказчика, не замерены (К-1); разрешённая мощность 15 кВт принята по типовым ТУ для квартиры, ТУ заказчиком не переданы (К-4); подрайон климата не задан — принят не северный (жилые от 2,5 м) (К-9).

Знак «**» — предложение проектировщика, заказчиком не утверждено (согласовать с заказчиком): пол пом. 1–3, 8, 9 — артикул выбран из каталога: Coswick 1167-1101 (инженерная доска, дуб натуральный, лак, 2100×127 мм); предложение исполнителя — выбор подтверждает автор; цены в каталоге нет, в смете «по КП».

См. лист открытых вопросов (лист 6, записи К-1, К-2, К-4; лист 7, запись К-9).

Изм.	Кол.уч	Лист	№ док.	Подп.	Дата
Разраб.		Кырлан А.С.			14.11.26
Пров.					
ГИП					
Н. контр.					
Утв.					

ГД-2026-007-АИ

Квартира 65 м²

Общая площадь 65,24* м² · * размеры со скана, не замерены (реестр — л. 6–8, К-1)

	Стадия	Лист	Листов
Дизайн-проект интерьера	РП	60	117
Спецификация отделочных материалов М б/м	**Кырлан Александр Сергеевич**		

Концепция декора и визуализации

Скандинавский · визуализации, палитра, материалы, ключевые предметы

ПРЕДВАРИТЕЛЬНО · не для производства работ · открыто пунктов: 14 (реестр — л. 6–8)



Визуализация 1. Вид сверху (3D): планировка с мебелью, текстилем и декором

Расстановка — по плану мебели (лист 25); шторы, ковры, картины и растения — по плану текстиля и декора (лист 62).



Визуализация 16. Кухня-гостиная (пом. 3)

шторы Т1**, Т2** · картина ДК1** · растение ДК2** · подушки, пледы Т3**, Т4**, Т5**




Визуализация 10. Спальня (пом. 2)

шторы Т6** · ковёр Т13** · картина ДК6** · зеркало ДК7** · подушки, пледы Т14**, Т15**, Т16**



Визуализация 14. Детская (пом. 9)

шторы Т7, Т8 · ковёр Т9 · картина ДК3 · зеркало ДК4 · подушки, пледы Т10, Т11, Т12

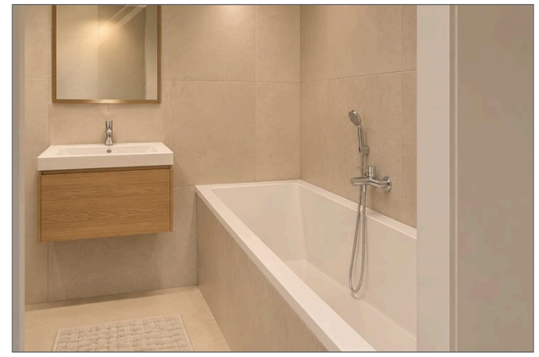

Визуализация 9. Ванная (пом. 7)

ковёр Т20** · зеркало ДК13** · подушки, пледы Т18**, Т19**

Материалы и фактуры



Дуб натуральный

пол: пом. 1, 2, 3, 8, 9; рамы ДК1**, ДК3, ДК6**, ДК7**, ДК8**, ДК9**,




Букле

подушки: Т3**, Т10, Т15**



Лён

римская штора, подушки, полотенца: Т1**, Т2**, Т4**, Т6**, Т7,

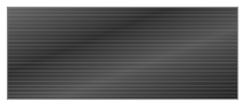

Чёрный матовый металл

рамы ДК4 — чёрный



Бархат

подушки: Т11

Ключевые предметы

— Диван М1** 2200×950 — кухня-гостиная; подушки и плед Т3**, Т4**, Т5**

— Кровати С1, С6 — над изголовьем картины ДК3; текстиль Т10, Т11, Т12, Т14**, Т15**, Т16**

— Ковры Т9, Т13**, Т17**, Т20** — шерсть, хлопок, хлопок тафтинг, на противоскользящей подложке

— Картины ДК1**, ДК3, ДК6**, ДК9**, ДК10**, ДК11**, ДК14** — центр на высоте 1500–1650 мм

— Зеркала в рост ДК4, ДК7**, ДК8**; над умывальниками ДК12**, ДК13**

— Шторы-волна Т7 (Tikkurila H487), тюль Т8 (Tikkurila V503) — в нишах потолка

— Растение ДК2**, ваза ДК5**

Настроение

Палитра выведена из выкрасов (колерная карта): база — тёплые нейтрали NCS S 1502-Y50R / S 1002-Y50R на стенах, NCS S 0300-N на потолках, Tikkurila V503 в гардеробной и детской; второй цвет — Farrow & Ball No. 241 (детская) и NCS S 0502-Y (кладовая); акцент — Farrow & Ball No. 30 Hague Blue (стена и текстиль детской). Настроение стиля: светло, спокойно, уютно (hygge), естественно, функционально, в меру (lagom). Свет тёплый, 2700–3000 K.

Примечания

1. Визуализации — образ интерьера. Изделия, размеры, высоты подвеса и привязки — по чертежам (план текстиля и декора — лист 62; шторы и карнизы — лист 63; ведомость текстиля — лист 64; ведомость декора и развеска — лист 65); при расхождении действуют чертежи и ведомости.
2. Коды цвета — ориентир подбора по веерам производителей; ткань утверждается по образцу при дневном свете и при свете проекта 2700–3000 K.
3. Мелкий стайлинг на визуализациях (книги, посуда, свечи) в ведомости не входит и поставляется заказчиком по желанию.

Палитра 60/30/10 и цвета текстиля



- NCS S 1502-Y50R (тёплый светло-серый), LRV 72 — 60 % база
- Tikkurila V503 (Winter), LRV 86 — 60 % база — Т8
- NCS S 0502-Y (белый сёдзи/сиккуй — известь, васи), LRV 86 — 30 % второй цвет
- Tikkurila G503 (Calla), LRV 89 — текстиль — Т1, Т2, Т3, Т6, Т15, Т19
- Farrow & Ball No. 231 (Setting Plaster), LRV 56 — текстиль — Т14
- NCS S 1002-Y50R (тёплый светлый грейж), LRV 82 — 60 % база
- Farrow & Ball No. 241 (Skimming Stone), LRV 67 — 30 % второй цвет — Т17, Т20
- Farrow & Ball No. 30 (Hague Blue), LRV 7 — 10 % акцент — Т12
- NCS S 2002-Y (серый камень, тёплый), LRV 55 — текстиль — Т13
- Farrow & Ball No. 299 (De Nimes), LRV 21 — акцент текстиля — Т4, Т16, Т18

Допущения и предложения на листе. Основа листа: размеры сняты с растрового плана заказчика без размеров: масштаб восстановлен по площадям помещений (≈ 11,8 мм на пиксель), контрольный обмер не выполнен (К-1); высота потолка 2700 мм принята: на плане заказчика её нет (К-2); толщины стен 300 / 120 мм приняты по плану заказчика, не замерены (К-1); разрешённая мощность 15 кВт принята по типовым ТУ для квартиры, ТУ заказчиком не переданы (К-4); подрайон климата не задан — принят не северный (жилые от 2,5 м) (К-9). Знак «**» — предложено, не утверждено (согласовать): К-5: М1. См. лист открытых вопросов (лист 6, записи К-1, К-2, К-4, К-5; лист 7, запись К-9; лист 8, записи ИЗ-4, ИЗ-5).

Изм.	Кол.уч	Лист	№ док.	Подп.	Дата
Разраб.		Кырлан А.С.			14.11.26
Пров.					
ГИП					
Н. контр.					
Утв.					

ГД-2026-007-АИ

Квартира 65 м²

Общая площадь 65,24* м² · * размеры со скана, не замерены (реестр — л. 6–8, К-1)

Дизайн-проект интерьера

Стадия	Лист	Листов
РП	61	117

Концепция декора и визуализации

М б/м


Кырлан Александр Сергеевич

выпуск 14.11.2026 № 9cc0b98f36 · стр. 68 из 139

План текстиля и декора

Шторы и карнизы, ковры, картины и зеркала, растения · размеры в мм от чистовых стен и чистого пола · марки — по ведомостям

ПРЕДВАРИТЕЛЬНО · не для производства работ · открыто пунктов: 14 (реестр — л. 6–8)

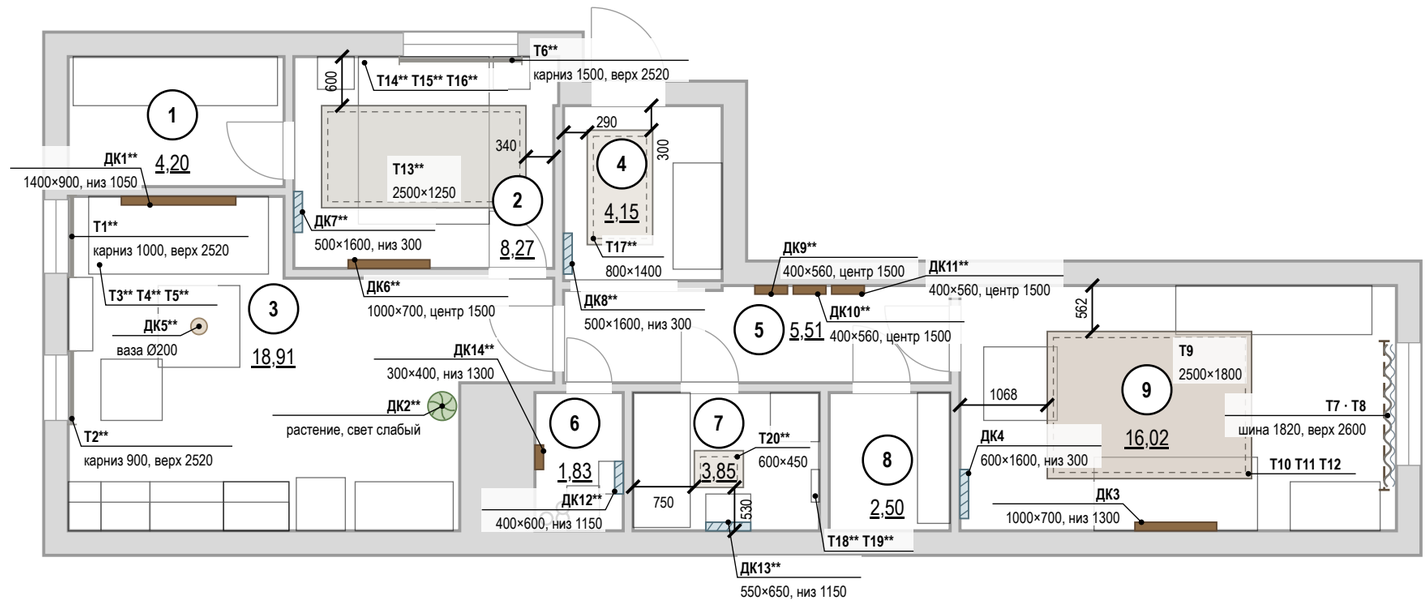

Условные обозначения

- ковёр — габарит в масштабе, цвет изделия
- шина или карниз штор (выше плоскости разреза)
- портьеры (штора-волна)
- тюль (на плане — волнистая линия)
- римская или рулонная штора в проёме
- картина на стене — ширина в масштабе
- зеркало на стене — ширина в масштабе
- растение в кашпо — диаметр в масштабе
- ваза, настольный декор
- подушки, пледы — марка на выноске к своей мебели
- привязка от чистовой стены, мм
- (1) номер помещения, площадь м²
- стены (подложка обмера)

T1, ДК1 — марки по ведомостям текстиля и декора

Экспликация помещений

лист 21 · на плане — номера в марках

Окна: шина → полотно, мм

Поз.	Шина	Верх шины	Полотно, низ
T6**	1500	2520	1750, низ 770
T1**	1000	2520	1750, низ 770
T2**	900	2520	1750, низ 770
T7, T8	1820	2600, ниша	2590, низ 10

Допущения и предложения на листе

Основа листа: размеры сняты с растрового плана заказчика без размеров: масштаб восстановлен по площадям помещений (≈ 11,8 мм на пиксель), контрольный обмер не выполнен (К-1); высота потолка 2700 мм принята: на плане заказчика её нет (К-2); толщины стен 300 / 120 мм приняты по плану заказчика, не замерены (К-1); разрешённая мощность 15 кВт принята по типовым ТУ для квартиры, ТУ заказчиком не переданы (К-4); подрайон климата не задан — принят не северный (жилые от 2,5 м) (К-9).

Знак «**» — предложение проектировщика, заказчиком не утверждено (согласовать с заказчиком): ИЗ-4: T6, T13, T14, T15, T16, ДК6, ДК7, T1, T2, T3, T4, T5, ДК1, ДК2, ДК5, T17, ДК8, ДК9, ДК10, ДК11, ДК12, ДК13; ИЗ-5: ДК14, T18, T19, T20.

Изменения по листу без подписи: ИЗ-4, ИЗ-5.

См. лист открытых вопросов (лист 6, записи К-1, К-2, К-4; лист 7, запись К-9; лист 8, записи ИЗ-4, ИЗ-5).

Примечания

1. Размеры — в мм. Отступы ковров — от чистовых стен; высоты картин и зеркал — от чистого пола до центра или низа рамы.
2. Шторы в пол — на шинах в нишах потолка (ниша — план потолков, лист 49); закладная под шину в нише — до обшивки ГКЛ. Римские шторы — на карнизах на стене над проёмом. Схемы окон, длины полотен и сборка — лист 63.
3. Картины и зеркала массой более 5 кг — на анкеры по основанию, нагрузка крепежа не меньше двойной массы изделия; на ГКЛ — только по закладной. Декор не перекрывает розетки и выключатели.
4. Ковры на гладком полу — на противоскользящей подложке.
5. Мебель — по плану расстановки мебели (лист 25); ведомость текстиля — лист 64, ведомость декора и схемы развески — лист 65.
6. Номера помещений — по экспликации (лист 21); наименования и площади на этом листе не дублируются.
7. Марки текстиля «Т» и декора «Д» относятся только к листам текстиля и декора; индексы трубопроводов Т1–Т4 — на листах ВК и ОВ.

1000 мм · печать 1:1

Изм.	Кол.уч	Лист	№ док.	Подп.	Дата
Разраб.		Кырлан А.С.			14.11.26
Пров.					
ГИП					
Н. контр.					
Утв.					

ГД-2026-007-АИ

Квартира 65 м²

Общая площадь 65,24* м² · * размеры со скана, не замерены (реестр — л. 6–8, К-1)

Дизайн-проект интерьера

Стадия	Лист	Листов
РП	62	117

План текстиля и декора

М 1:75

Кырлан Александр Сергеевич

выпуск 14.11.2026 № 9cc0b98f36 · стр. 69 из 139

08

Декор и текстиль


Кырлан Александр Сергеевич

выпуск 14.11.2026 № 9cc0b98f36 · стр. 70 из 139


Шторы и карнизы

Схемы окон «шина → полотно» (М 1:50) · отметки от чистого пола помещения · размеры в мм


Окно 1 — Спальня (пом. 2): Т6 (М 1:50)**

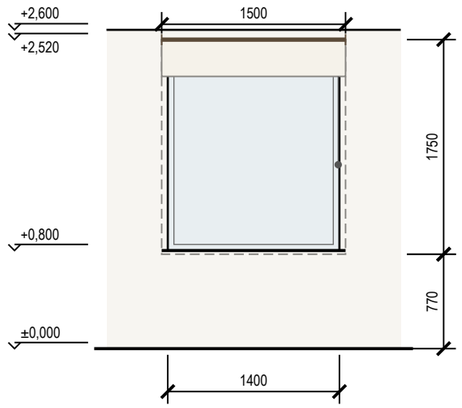


Окно 1 — Кухня-гостиная (пом. 3): Т1 (М 1:50)**

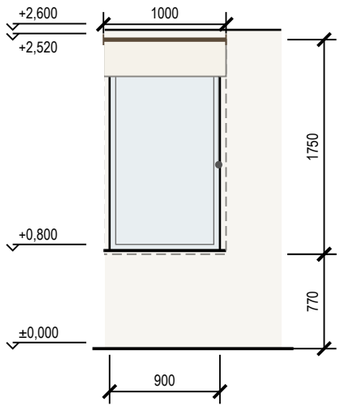

Окно 2 — Кухня-гостиная (пом. 3): Т2 (М 1:50)**

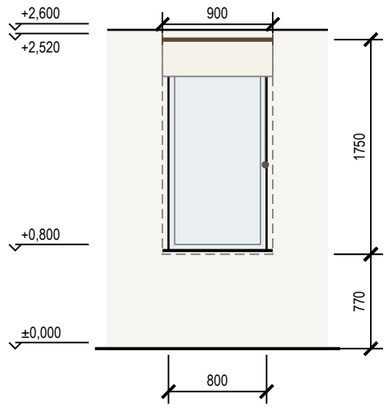

Окно 1 — Детская (пом. 9): Т7, Т8 (М 1:50)

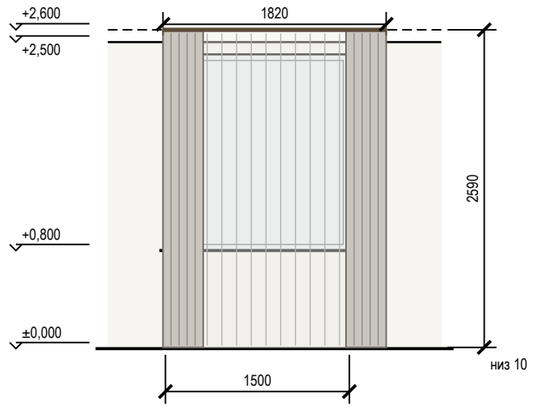

Карта окон: окно → шина → полотно

Поз.	Окно, пом.	Проём Ш×В, подоконник	Верх ниши	Изделие	Шина / карниз: длина, крепление	Верх шины	Полотно: длина, низ	Управление
Т6**	1, пом. 2	1400×1600, подок. 800		римская штора	карниз, 1500, на стену, вынос 60	+2,520	1750, низ 770	шнур, петля низом 1500, натяжитель
Т1**	1, пом. 3	900×1600, подок. 800		римская штора	карниз, 1000, на стену, вынос 60	+2,520	1750, низ 770	шнур, петля низом 1500, натяжитель
Т2**	2, пом. 3	800×1600, подок. 800		римская штора	карниз, 900, на стену, вынос 60	+2,520	1750, низ 770	шнур, петля низом 1500, натяжитель
Т7	1, пом. 9	1500×1600, подок. 800	+2,600	портьеры	шина, 1820, в нише потолка, вынос 150	+2,600	2590, низ 10 (парит)	вручную
Т8	1, пом. 9	1500×1600, подок. 800	+2,600	тюль	шина, 1820, в нише потолка, вынос 150	+2,600	2590, низ 10 (парит)	вручную

Задания смежникам

Кому	Задание	Пом.
Гипсокартонщик	окно 1 (1500×1600, Т7, Т8): ниша под шторы 150×100, верх +2,600; закладная под шину L 1820 по всей длине — до обшивки	9
Электрик	выводы под электрокарнизы не требуются (управление вручную)	

Условные обозначения

- портьеры в открытом положении
- римская штора: сложена / опущена
- верх ниши под шторы в потолке
- тюль (на виде окна — прозрачная плашка)
- шина или карниз на отметке верха
- оконный проём

Допущения и предложения на листе

Основа листа: размеры сняты с растрового плана заказчика без размеров: масштаб восстановлен по площадям помещений (≈ 11,8 мм на пиксель), контрольный обмер не выполнен (К-1); высота потолка 2700 мм принята: на плане заказчика её нет (К-2); толщины стен 300 / 120 мм приняты по плану заказчика, не замерены (К-1); разрешённая мощность 15 кВт принята по типовым ТУ для квартиры, ТУ заказчиком не переданы (К-4); подрайон климата не задан — принят не северный (жилые от 2,5 м) (К-9).
Знак «**» — предложение проектировщика, заказчиком не утверждено (согласовать с заказчиком): ИЗ-4: Т6, Т1, Т2.
Изменения по листу без подписи: ИЗ-4.
См. лист открытых вопросов (лист 6, записи К-1, К-2, К-4; лист 7, запись К-9; лист 8, запись ИЗ-4).

Примечания

1. Отметки — от чистого пола помещения; размеры — мм.
2. Шины в нишах потолка (Т7, Т8): закладная (брус или профиль) по всей длине ниши — до обшивки ГКЛ; ниша и её отметка — узел ниши на плане потолков (лист 49).
3. Шина в нише — на отметке верха ниши (крепление к закладной в потолке ниши); длина полотна — от верха шины до чистого пола за вычетом зазора.
4. Карнизы на стене над проёмом (Т1**, Т2**, Т6**) — на анкеры по основанию; на ГКЛ — только по закладной.
5. Полотно портьер «парит» над полом на 10 мм; сборка портьер — 2,0, тюля — 2,5 (ширина полотна — в ведомости текстиля).
6. Шнур римской шторы — с натяжителем, петля низом не ниже 1500 мм от пола (защита детей; EN 13120 — рекомендация).
7. Электрокарнизы не предусмотрены; при замене на электропривод — вывод кабеля у края шины (задание электрику).
8. Марки изделий — по плану текстиля и декора (лист 62) и ведомости текстиля (лист 64).

Изм.	Кол.уч	Лист	№ док.	Подп.	Дата
Разраб.		Кырлан А.С.			14.11.26
Пров.					
ГИП					
Н. контр.					
Утв.					

ГД-2026-007-АИ

Квартира 65 м²

Общая площадь 65,24* м² · * размеры со скана, не замерены (реестр — л. 6–8, К-1)

Дизайн-проект интерьера

Стадия	Лист	Листов
РП	63	117

Шторы и карнизы

М б/м

Кырлан Александр Сергеевич

выпуск 14.11.2026 № 9cc0b98f36 · стр. 71 из 139

ПРЕДВАРИТЕЛЬНО · не для производства работ · открыто пунктов: 14 (реестр — л. 6–8)

Ведомость текстиля

Шторы, тюль, римские шторы, ковры, подушки и пледы · размеры в мм · марки — по плану текстиля и декора

Текстиль: шторы, ковры, подушки, пледы

Поз.	Пом.	Изделие	Размер, мм	Ткань, состав, плотность	Сборка, ширина полотна		Цвет (система, код)	Кол.	Примечание
T1**	3	Римская штора льняная, молочная (окно 1)	карниз 1000 × полотно 1750	лён 100 %			Tikkurila G503 (Calla)	1	низ 770; на стену; шнур: петля 1500, натяжитель
T2**	3	Римская штора льняная, молочная (окно 2)	карниз 900 × полотно 1750	лён 100 %			Tikkurila G503 (Calla)	1	низ 770; на стену; шнур: петля 1500, натяжитель
T3**	3	Подушки на диван, букле молочное	500×500	букле (шерсть 60 %, полиэстер 40 %)			Tikkurila G503 (Calla)	3	на M1**
T4**	3	Подушки на диван, лён, приглушённый синий	400×600	лён 100 %			Farrow & Ball No. 299 (De Nimes)	2	на M1**
T5**	3	Плед шерстяной на диван, терракота	1300×1700	шерсть мериноса 100 %			NCS S 3020-Y80R (приглушённая терракота/пудра)	1	на M1**
T6**	2	Римская штора льняная с блэкаут-подкладкой, молочная	карниз 1500 × полотно 1750	лён с блэкаут-подкладкой; лён 100 %			Tikkurila G503 (Calla)	1	низ 770; на стену; шнур: петля 1500, натяжитель
T7	9	Портьеры-волна	шина 1820 × полотно 2590	лён с блэкаут-подкладкой; лён 100 %; 320 г/м²	× 2, ширина 3640		Tikkurila H487 (Pumice)	2	низ 10 (парит); в нише потолка
T8	9	Тюль	шина 1820 × полотно 2590	вуаль; полиэстер 100 %	× 2,5, ширина 4550		Tikkurila V503 (Winter)	1	низ 10 (парит); в нише потолка
T9	9	Ковёр под кроватью	2500×1800	шерсть, плоское плетение; шерсть 100 %			Tikkurila V484 (Driftwood)	1	противоскользящая подложка; ворс 8 мм
T10	9	Подушки декоративные на кровать	500×500	букле (шерсть 60 %, полиэстер 40 %)			Farrow & Ball No. 229 (Elephant's Breath)	3	на C6
T11	9	Подушки на кровать, акцент	400×600	хлопковый бархат 100 %			Farrow & Ball No. 47 (Green Smoke)	2	на C6
T12	9	Плед на кровать	1300×1700	шерсть мериноса 100 %			Farrow & Ball No. 30 (Hague Blue)	1	на C6
T13**	2	Ковёр шерстяной 2500×1250 под кроватью, выходит по бокам на 450 мм, овсяный	2500×1250	шерсть, плоское плетение; шерсть 100 %			NCS S 2002-Y (серый камень, тёплый)	1	противоскользящая подложка; ворс 6 мм
T14**	2	Подушки декоративные на кровать, лён, пыльно-розовый	500×500	лён 100 %			Farrow & Ball No. 231 (Setting Plaster)	2	на C1
T15**	2	Подушка-валик на кровать, букле молочное	350×550	букле (шерсть 60 %, полиэстер 40 %)			Tikkurila G503 (Calla)	1	на C1
T16**	2	Плед шерстяной в изножье кровати, приглушённый синий	1300×1700	шерсть мериноса 100 %			Farrow & Ball No. 299 (De Nimes)	1	на C1
T17**	4	Дорожка-коврик хлопковая тканая 800×1400, светлая	800×1400	хлопок, ручное ткачество; хлопок 100 %			Farrow & Ball No. 241 (Skimming Stone)	1	противоскользящая подложка; ворс 4 мм
T18**	7	Полотенца банные махровые, приглушённый синий, сложены на полотенцесушителе	700×1400	махра; хлопок 100 %; 550 г/м²			Farrow & Ball No. 299 (De Nimes)	2	на П5; уход: 40 °C, без кондиционера
T19**	7	Полотенца для рук вафельные, молочные, на нижних перекладинах сушителя	500×900	вафельное полотно; хлопок 100 %; 280 г/м²			Tikkurila G503 (Calla)	2	на П5; уход: 60 °C
T20**	7	Коврик для ванной у бортика ванны, хлопок тафтинг, светлый каменный	600×450	хлопок 100 %, латексная противоскользящая основа			Farrow & Ball No. 241 (Skimming Stone)	1	противоскользящая подложка; ворс 12 мм; уход: 40 °C

образец цвета — по HEX производителя краски, справочно

Итого: шторы и тюль — 6 шт.; подушки, пледы, покрывала — 20 шт.; ковры и дорожки — 4 шт.

Примечания

1. Коды цвета — ориентир подбора по веерам производителей красок; ткань утверждается по образцу при дневном свете и при свете проекта 2700–3000 K.
2. Размеры полотен — по замеру после чистовой отделки пола и потолка; ширина полотна указана с учётом сборки, без припусков на швы. Схемы окон и отметки шин лист 63.
3. Портьеры и тюль — на тесьме «волна» по системе шины; блэкаут — подкладкой. Ковры — на противоскользящей подложке.
4. Замена изделия — аналогом по характеристикам (состав, плотность, размер, цвет по образцу) с согласованием автора проекта.
5. Места изделий — план текстиля и декора (лист 62); подушки и пледы — по марке мебели.

Допущения и предложения на листе. Основа листа: размеры сняты с растрового плана заказчика без размеров: масштаб восстановлен по площадям помещений (≈ 11,8 мм на пиксель), контрольный обмер не выполнен (К-1); высота потолка 2700 мм принята: на плане заказчика её нет (К-2); толщины стен 300 / 120 мм приняты по плану заказчика, не замерены (К-1); разрешённая мощность 15 кВт принята по типовым ТУ для квартиры, ТУ заказчиком не переданы (К-4); подрайон климата не задан — принят не северный (жилые от 2,5 м) (К-9). Знак «**» — предложение проектировщика, заказчиком не утверждено (согласовать с заказчиком): К-5: М1 — Было х 2900, у 3000 — в полосе 1400 мм между спальней и кухней, единственном проходе от двери Д-2: стыки частей 290 / 200 / 0 мм (→). См. лист открытых вопросов (лист 6, записи К-1, К-2, К-4, К-5; лист 7, запись К-9; лист 8, записи ИЗ-4, ИЗ-5); по листу — ИЗ-4, ИЗ-5.

Изм.	Кол.уч	Лист	№ док.	Подп.	Дата
Разраб.		Кырлан А.С.			14.11.26
Пров.					
ГИП					
Н. контр.					
Утв.					

ГД-2026-007-АИ

Квартира 65 м²

Общая площадь 65,24* м² · * размеры со скана, не замерены (реестр — л. 6–8, К-1)

Дизайн-проект интерьера

Стадия	Лист	Листов
РП	64	117

Ведомость текстиля

М б/м

Кырлан Александр Сергеевич

выпуск 14.11.2026 № 9cc0b98f36 · стр. 72 из 139

Ведомость декора

Картины, зеркала, растения, настольный декор · высоты — мм от чистого пола

Декор: картины, зеркала, растения, предметы

Поз.	Пом.	Предмет	Размер, мм	Место: стена, высота от пола, мм	Масса, кг	Крепёж и основание	Свет места, отделка	Кол.
ДК1**	3	Картина над диваном: Северное море: широкие горизонтальные мазки серо-синего и песочного, холст	1400×900	стена А, привязка 650; низ 1050, центр 1500; над М1**	6	анкер, 2 шт.; основание: бетон; нагрузка 20 кг	рама — дуб	1
ДК2**	3	Сансевиерия в напольном керамическом кашпо Ø300, матовый белый	350×350	напольное			свет слабый	1
ДК3	9	Картина над кроватью: Кит и маленькая лодка, детская иллюстрация, гуашь	1000×700	стена В, привязка 2140; низ 1300, центр 1650; над С6	4	подвес по основанию, 2 точки	рама — дуб	1
ДК4	9	Зеркало в рост в тонкой чёрной раме	600×1600	стена Г, привязка 2250; низ 300, центр 1100	12	анкер для пустотелых оснований, 4 шт.; основание: перегородка — определить обмером до монтажа; нагрузка 30 кг	рама — чёрный матовый металл	1
ДК5**	3	Ваза керамическая матовая с сухой веткой на обеденном столе, молочная	200×300	на М2** (обеденный стол)				1
ДК6**	2	Картина напротив кровати: Полевые травы, гербарий, акварель	1000×700	стена В, привязка 665; центр 1500	4	дюбель с крюком, 2 точки; основание: перегородка — определить обмером до монтажа; нагрузка 10 кг	рама — дуб	1
ДК7**	2	Зеркало в рост в тонкой дубовой раме 500×1600	500×1600	стена Г, привязка 1650; низ 300, центр 1100	12	анкер для пустотелых оснований, 4 шт.; основание: перегородка — определить обмером до монтажа; нагрузка 30 кг	рама — дуб	1
ДК8**	4	Зеркало в рост в дубовой раме 500×1600	500×1600	стена Г, привязка 1560; низ 300, центр 1100	12	анкер для пустотелых оснований, 4 шт.; основание: перегородка — определить обмером до монтажа; нагрузка 30 кг	рама — дуб	1
ДК9**	5	Постер в дубовой раме 400×560, левый (группа «триптих»): Сосна, линейный рисунок тушью	400×560	стена А, привязка 400; центр 1500	2	дюбель с крюком, 2 точки; основание: перегородка — определить обмером до монтажа; нагрузка 10 кг	рама — дуб	1
ДК10**	5	Постер в дубовой раме 400×560, средний (группа «триптих»): Берёзовая роща, линейный рисунок тушью	400×560	стена А, привязка 870; центр 1500	2	дюбель с крюком, 2 точки; основание: перегородка — определить обмером до монтажа; нагрузка 10 кг	рама — дуб	1
ДК11**	5	Постер в дубовой раме 400×560, правый (группа «триптих»): Озеро и ельник на дальнем берегу, рисунок тушью	400×560	стена А, привязка 1340; центр 1500	2	дюбель с крюком, 2 точки; основание: перегородка — определить обмером до монтажа; нагрузка 10 кг	рама — дуб	1
ДК12**	6	Зеркало над умывальником, влагостойкое, в тонкой дубовой раме 400×600	400×600	стена Б, привязка 840; низ 1150, центр 1450; над П21	5	клей для зеркал + 2 опорных уголка снизу; основание: стена под керамогранитом — основание — определить обмером до монтажа; нагрузка 15 кг		1
ДК13**	7	Зеркало над умывальником, влагостойкое, в тонкой дубовой раме 550×650	550×650	стена В, привязка 890; низ 1150, центр 1475; над П3	5	клей для зеркал + 2 опорных уголка снизу; основание: стена под керамогранитом — основание — определить обмером до монтажа; нагрузка 15 кг		1
ДК14**	6	Постер в тонкой дубовой раме 300×400: Чайка над водой, линейный рисунок тушью	300×400	стена Г, привязка 640; низ 1300, центр 1500	1	дюбель с крюком, 1 точка; основание: стена под керамогранитом — основание — определить обмером до монтажа; нагрузка 5 кг	рама — дуб	1

Допущения и предложения на листе

Основа листа: размеры сняты с растрового плана заказчика без размеров: масштаб восстановлен по площадям помещений (≈ 11,8 мм на пиксель), контрольный обмер не выполнен (К-1); высота потолка 2700 мм принята: на плане заказчика её нет (К-2); толщины стен 300 / 120 мм приняты по плану заказчика, не замерены (К-1); разрешённая мощность 15 кВт принята по типовым ТУ для квартиры, ТУ заказчиком не переданы (К-4); подрайон климата не задан — принят не северный (жилые от 2,5 м) (К-9).

Знак «**» — предложение проектировщика, заказчиком не утверждено (согласовать с заказчиком): ИЗ-4: ДК6, ДК7, ДК1, ДК2, ДК5, ДК8, ДК9, ДК10, ДК11, ДК12, ДК13; ИЗ-5: ДК14; К-5: М2 — Было х 1000, у 2700; М1 — Было х 2900, у 3000 — в полосе 1400 мм между спальней и кухней, единственном проходе от двери Д-2: стыки частей 290 / 200 / 0 мм (→).

Изменения по листу без подписи: ИЗ-4, ИЗ-5.

См. лист открытых вопросов (лист 6, записи К-1, К-2, К-4, К-5; лист 7, запись К-9; лист 8, записи ИЗ-4, ИЗ-5).

Примечания

1. Высоты — от чистого пола помещения до низа изделия, «ц» — до центра; привязки — от чистовой грани угла стены, мм.
2. Над мебелью низ изделия — на 150–250 мм выше спинки или изголовья; без мебели центр — на 1450–1600 мм от пола.
3. Изделия до 5 кг — на два подвеса по основанию; тяжелее — на анкеры с нагрузкой не меньше двойной массы; на ГКЛ — только по закладной или анкеру для пустотелых оснований.
4. Зеркала в рост — с креплением от опрокидывания; в санузлах — влагостойкие, на клей для зеркал и нейтральный силикон.
5. Места изделий — план текстиля и декора (лист 62). Схемы развески — лист 66.

Изм.	Кол.уч	Лист	№ док.	Подп.	Дата
Разраб.		Кырлан А.С.			14.11.26
Пров.					
ГИП					
Н. контр.					
Утв.					

ГД-2026-007-АИ

Квартира 65 м²

Общая площадь 65,24* м² · * размеры со скана, не замерены (реестр — л. 6–8, К-1)

Дизайн-проект интерьера

Стадия	Лист	Листов
РП	65	117

Ведомость декора

М б/м

Кырлан Александр Сергеевич

выпуск 14.11.2026 № 9cc0b98f36 · стр. 73 из 139

Схемы развески


Схемы развески картин и зеркал (М 1:50) · высоты — мм от чистого пола

ПРЕДВАРИТЕЛЬНО · не для производства работ · открыто пунктов: 14 (реестр — л. 6–8)


Ведомость декора (размер, масса, крепёж и основание) — лист 65

картина · зеркало · мебель под изделием


ДК1 — Кухня-гостиная (пом. 3), стена А (М 1:50)**

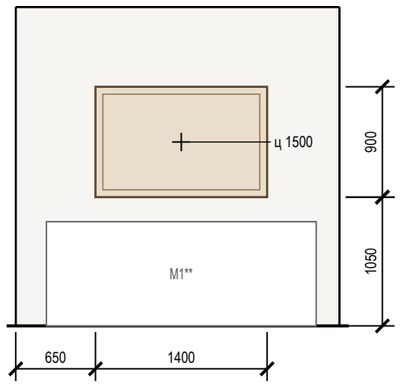


ДК3 — Детская (пом. 9), стена В (М 1:50)

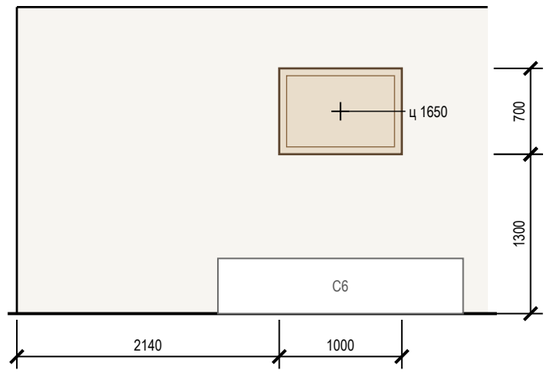


ДК4 — Детская (пом. 9), стена Г (М 1:50)

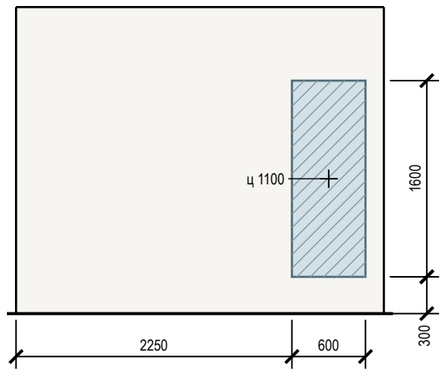


ДК6 — Спальня (пом. 2), стена В (М 1:50)**

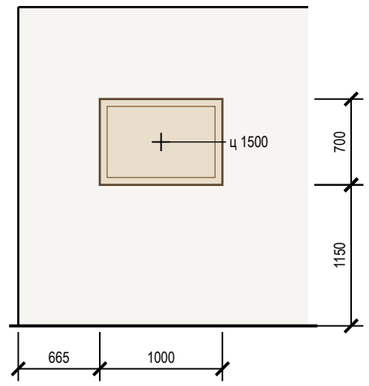


ДК7 — Спальня (пом. 2), стена Г (М 1:50)**

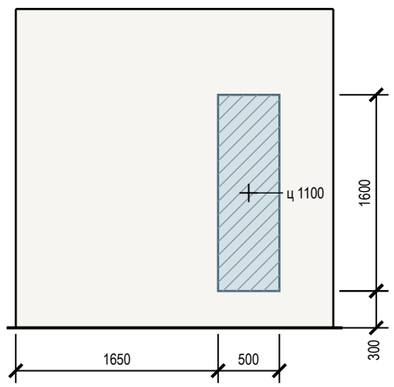


ДК8 — Прихожая (пом. 4), стена Г (М 1:50)**

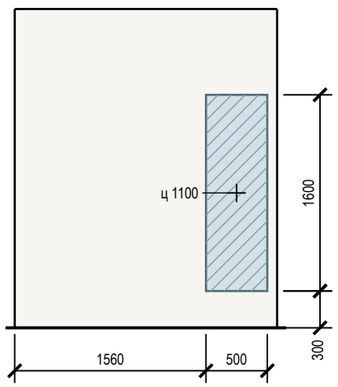


ДК9, ДК10**, ДК11** — Коридор (пом. 5), стена А, группа «триптих» (М 1:50)**

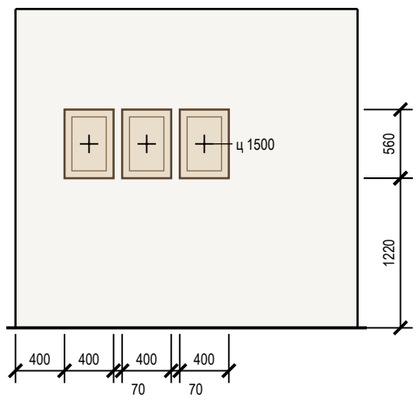


ДК12 — Санузел (пом. 6), стена Б (М 1:50)**

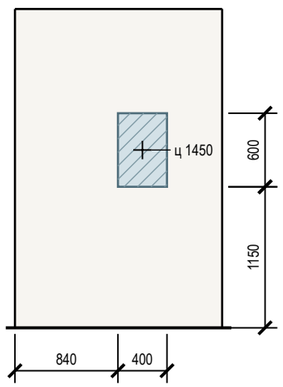

ДК13 — Ванная (пом. 7), стена В (М 1:50)**

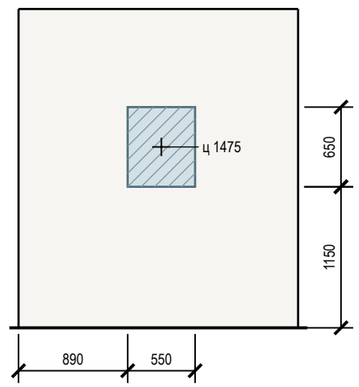

ДК14 — Санузел (пом. 6), стена Г (М 1:50)**

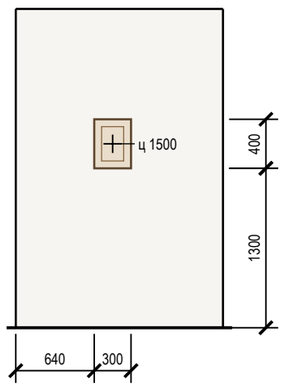

Допущения и предложения на листе

Основа листа: размеры сняты с растрового плана заказчика без размеров: масштаб восстановлен по площадям помещений (≈ 11,8 мм на пиксель), контрольный обмер не выполнен (К-1); высота потолка 2700 мм принята: на плане заказчика её нет (К-2); толщины стен 300 / 120 мм приняты по плану заказчика, не замерены (К-1); разрешённая мощность 15 кВт принята по типовым ТУ для квартиры, ТУ заказчиком не переданы (К-4); подрайон климата не задан — принят не северный (жилые от 2,5 м) (К-9).

Знак «**» — предложение проектировщика, заказчиком не утверждено (согласовать с заказчиком): ИЗ-4: ДК6, ДК7, ДК1, ДК8, ДК9, ДК10, ДК11, ДК12, ДК13; ИЗ-5: ДК14; К-5: М1 — Было х 2900, у 3000 — в полосе 1400 мм между спальней и кухней, единственном проходе от двери Д-2: стыки частей 290 / 200 / 0 мм (→).

См. лист открытых вопросов (лист 6, записи К-1, К-2, К-4, К-5; лист 7, запись К-9; лист 8, записи ИЗ-4, ИЗ-5).

Примечания

1. Высоты — от чистого пола помещения до низа изделия, «ц» — до центра; привязки — от чистовой грани угла стены, мм.
2. Над мебелью низ изделия — на 150–250 мм выше спинки или изголовья; без мебели центр — на 1450–1600 мм от пола.
3. Изделия до 5 кг — на два подвеса по основанию; тяжелее — на анкеры с нагрузкой не меньше двойной массы; на ГКЛ — только по закладной или анкеру для пустотелых оснований.
4. Зеркала в рост — с креплением от опрокидывания; в санузлах — влагостойкие, на клей для зеркал и нейтральный силикон.
5. Места изделий — план текстиля и декора (лист 62). Ведомость декора: размер, масса, крепёж и основание — лист 65.

Изм.	Кол.уч	Лист	№ док.	Подп.	Дата
Разраб.		Кырлан А.С.			14.11.26
Пров.					
ГИП					
Н. контр.					
Утв.					

ГД-2026-007-АИ

Квартира 65 м²

Общая площадь 65,24* м² · * размеры со скана, не замерены (реестр — л. 6–8, К-1)

Дизайн-проект интерьера

Стадия	Лист	Листов
РП	66	117

Схемы развески

М б/м

Кырлан Александр Сергеевич

выпуск 14.11.2026 № 9cc0b98f36 · стр. 74 из 139

Встроенная мебель. Схема расположения

встроенная и корпусная мебель на заказ, кухонный гарнитур · размеры в мм · марки — по ведомости изделий

ПРЕДВАРИТЕЛЬНО · не для производства работ · открыто пунктов: 14 (реестр — л. 6–8)



Ведомость изделий

Марка	Наименование	Пом.	Ш×Г×В, мм	Лист
Г1	Система хранения	1	2500×600×2400	68
M11	Шкаф-купе	4	1300×600×2500	69
Г2	Система хранения	8	1600×400×2400	70
C5	Шкаф распашной	9	2400×600×2400	71
M8	Место под холодильник отдельностоящий: без корпуса и фасада	3	600×650×2100	72, 73
M6	Модуль нижний: мойка	3	800×600×900	72, 73
M9	Модуль навесной: сушка, полки	3	1700×350×720	72, 73
M7	Модуль нижний: ящики	3	900×600×900	72, 73
M5	Модуль нижний: ящики, варочная	3	600×600×900	72, 73
M13	Модуль навесной: полки	3	600×350×620	72, 73
M4	Модуль нижний: ящики	3	400×600×900	72, 73
M12	Модуль навесной: полки	3	400×350×720	72, 73

Условные обозначения

- изделие мебельщика: корпус на полу
- невидимый контур: навесной модуль, корпус под столешницей
- открывание распашного фасада
- зона выдвижения ящика, двери техники
- дверь купе, стрелка — направление движения
- К1 — марка изделия или модуля (на схеме расположения под ней — лист изделия)

Примечания

1. Изделия — по чистовым размерам помещений; перед раскроем — контрольный замер цеха после чистовой отделки стен, пола и потолка.
2. Открывание фасадов и выдвижение ящиков показано в открытом положении: зоны не пересекают двери, радиаторы, выключатели и проходы.
3. Стояки и счётчики за мебелью — с сервисным люком; газовые трубы мебелью не зашиваются.
4. Покупная мебель — по плану расстановки мебели и спецификации дизайнера; здесь — подложкой.

Допущения и предложения на листе

Основа листа: размеры сняты с растрового плана заказчика без размеров: масштаб восстановлен по площадям помещений (≈ 11,8 мм на пиксель), контрольный обмер не выполнен (К-1); высота потолка 2700 мм принята: на плане заказчика её нет (К-2); толщины стен 300 / 120 мм приняты по плану заказчика, не замерены (К-1); разрешённая мощность 15 кВт принята по типовым ТУ для квартиры, ТУ заказчиком не переданы (К-4); подрайон климата не задан — принят не северный (жилые от 2,5 м) (К-9).
См. лист открытых вопросов (лист 6, записи К-1, К-2, К-4; лист 7, запись К-9).

1000 мм · печать 1:1

Изм.	Кол.уч	Лист	№ док.	Подп.	Дата
Разраб.		Кырлан А.С.			14.11.26
Пров.					
ГИП					
Н. контр.					
Утв.					

ГД-2026-007-АИ

Квартира 65 м²

Общая площадь 65,24* м² · * размеры со скана, не замерены (реестр — л. 6–8, К-1)

Дизайн-проект интерьера

Стадия	Лист	Листов
РП	67	117

Встроенная мебель. Схема расположения

М 1:75

Кырлан Александр Сергеевич


выпуск 14.11.2026 № 9cc0b98f36 · стр. 75 из 139

Система хранения Г1


Гардеробная (пом. 1) · вид из помещения · размеры в мм, отметки в м

ПРЕДВАРИТЕЛЬНО · не для производства работ · открыто пунктов: 14 (реестр — л. 6–8)


Общий вид (М 1:40)

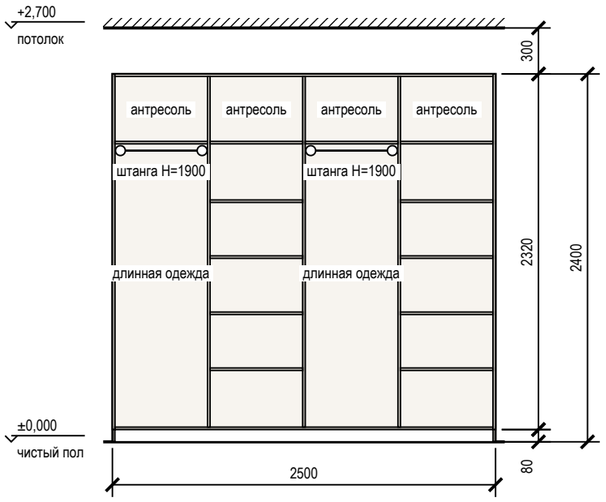


Наполнение, размеры в свету (М 1:40)

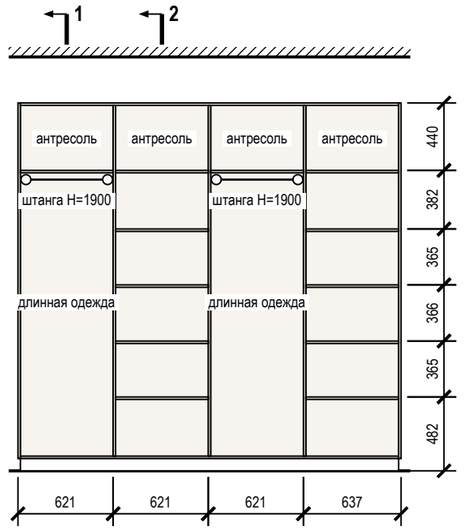

Разрез 1-1 (М 1:40)

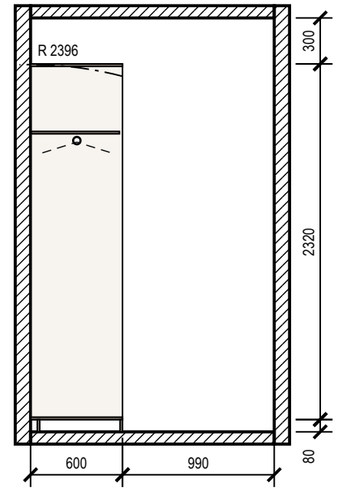

Разрез 2-2 (М 1:40)

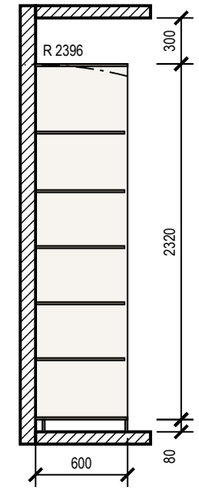

Примечания

1. Размеры — в мм по чистовой отделке; изделие 2500×600×2400 (Ш×Г×В). Перед раскроем — контрольный замер цеха после чистовой отделки стен, пола и потолка.
2. Корпус — ЛДСП 16 мм, задняя стенка ХДФ 4 мм в паз, цоколь 80 мм на регулируемых опорах; открытая система: без фасадов.
3. Кромка: скрытые торцы 0,4 мм, видимые 2 мм (ПВХ/АБС).
4. Присадка по 32-й системе — выполняет цех.
5. Зазор до потолка 300 мм.
6. Подъём корпуса: диагональ боковины без цоколя $\sqrt{(2320^2 + 600^2)}$ = 2396 мм < 2700 мм до потолка — корпус собирается лёжа, поднимается поворотом и ставится на цоколь.
7. Крепление к стене от опрокидывания: крепление к стене, 3 точки; основание стены и шаг анкеров — монтажная схема шкафов.
8. Проход перед изделием 990 мм показан на разрезе 1-1.

Условные обозначения

- корпус и полки ЛДСП (вид на стену)
- задняя стенка ХДФ
- деталь в разрезе
- штанга для плечиков (на разрезе — плечики 450 мм)
- траектория угла корпуса при подъёме в проектное положение

Допущения и предложения на листе

Основа листа: размеры сняты с растрового плана заказчика без размеров: масштаб восстановлен по площадям помещений (≈ 11,8 мм на пиксель), контрольный обмер не выполнен (К-1); высота потолка 2700 мм принята: на плане заказчика её нет (К-2); толщины стен 300 / 120 мм приняты по плану заказчика, не замерены (К-1); разрешённая мощность 15 кВт принята по типовым ТУ для квартиры, ТУ заказчиком не переданы (К-4); подрайон климата не задан — принят не северный (жилые от 2,5 м) (К-9).
См. лист открытых вопросов (лист 6, записи К-1, К-2, К-4; лист 7, запись К-9).

1000 мм · печать 1:1

Изм.	Кол.уч	Лист	№ док.	Подп.	Дата
Разраб.		Кырлан А.С.			14.11.26
Пров.					
ГИП					
Н. контр.					
Утв.					

ГД-2026-007-АИ

Квартира 65 м²

Общая площадь 65,24* м² · * размеры со скана, не замерены (реестр — л. 6–8, К-1)

Дизайн-проект интерьера

Стадия	Лист	Листов
РП	68	117

Система хранения Г1

М 1:40

Кырлан Александр Сергеевич


выпуск 14.11.2026 № 9cc0b98f36 · стр. 76 из 139

Шкаф-купе М11


Прихожая (пом. 4) · вид из помещения · размеры в мм, отметки в м

ПРЕДВАРИТЕЛЬНО · не для производства работ · открыто пунктов: 14 (реестр — л. 6–8)


Вид с фасадами (М 1:20)

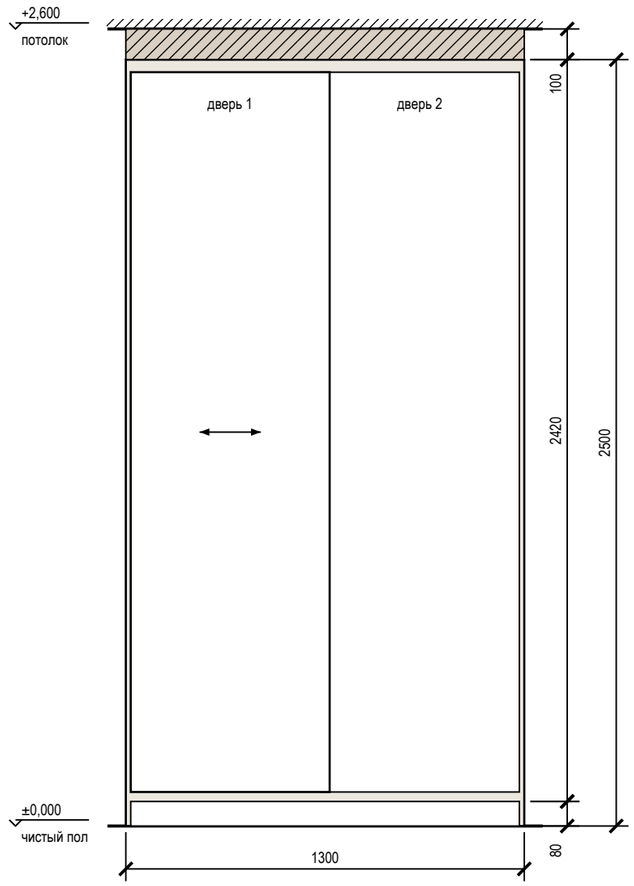


Вид без фасадов (М 1:20)

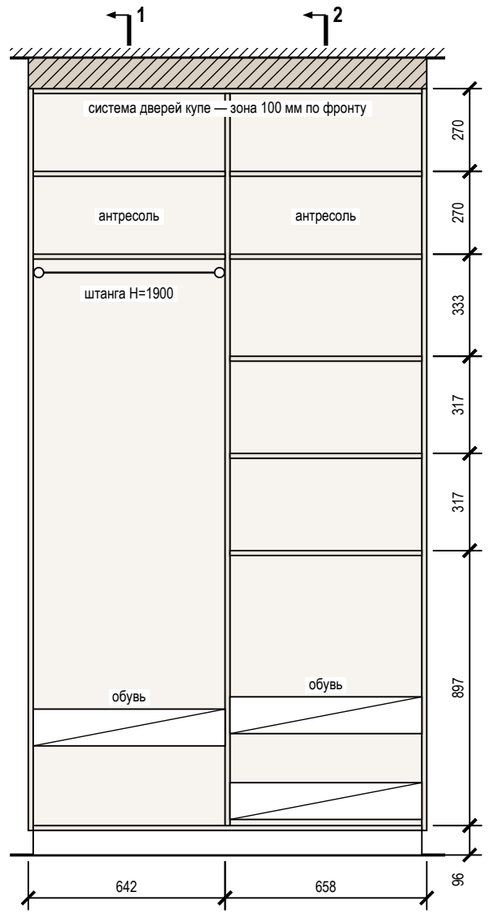

Разрез 1-1 (М 1:20)

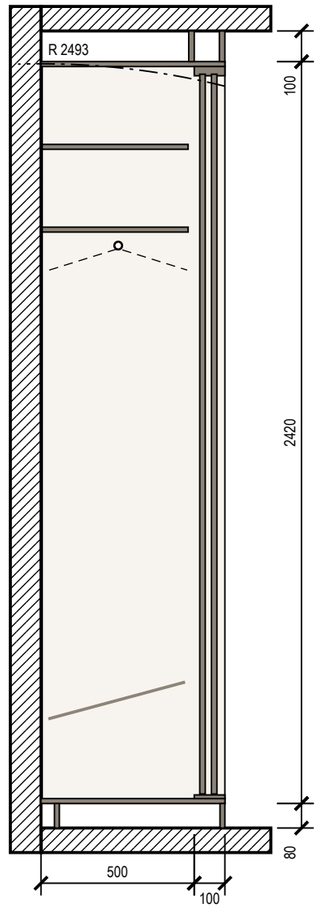

Разрез 2-2 (М 1:20)

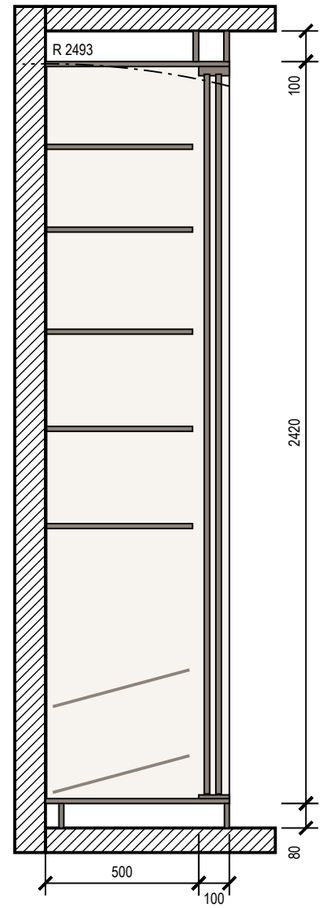

Примечания

1. Размеры — в мм по чистовой отделке; изделие 1300×600×2500 (Ш×Г×В). Перед раскроем — контрольный замер цеха после чистовой отделки стен, пола и потолка.
2. Корпус — ЛДСП 16 мм, задняя стенка ХДФ 4 мм в паз, цоколь 80 мм на регулируемых опорах; двери купе — ЛДСП 10 мм в алюминиевом профиле; нахлёст 30 мм, ширина двери 649 мм, высота — проём минус 40 мм; цвет — по колерной карте.
3. Кромка: скрытые торцы 0,4 мм, видимые 1 мм (ПВХ/АБС).
4. Номинальные зазоры: дверь купе — боковина 3 мм, фасад ящика — стойка 2 мм; ящики внутри купе — с накладкой 30 мм на стойке со стороны нахлёста дверей.
5. Присадка по 32-й системе — выполняет цех.
6. Компенсатор 100 мм — короб из ЛДСП по фронту и торцам, подгоняется к потолку при монтаже (припуск 20 мм), крепится к корпусу и к потолку.
7. Подъём корпуса: диагональ боковины без цоколя √(2420² + 600²) = 2493 мм < 2600 мм до потолка — корпус собирается лёжа, поднимается поворотом и ставится на цоколь.
8. Крепление к стене от опрокидывания — уголки 2 шт. к несущему основанию (монтажная схема шкафов).

Условные обозначения

- дверь купе, стрелка — направление движения
- корпус и полки ЛДСП (вид на стену)
- задняя стенка ХДФ
- деталь в разрезе
- компенсатор — короб до потолка
- штанга для плечиков (на разрезе — плечики 450 мм)
- траектория угла корпуса при подъёме в проектное положение

Допущения и предложения на листе

Основа листа: размеры сняты с растрового плана заказчика без размеров: масштаб восстановлен по площадям помещений (≈ 11,8 мм на пиксель), контрольный обмер не выполнен (К-1); высота потолка 2700 мм принята: на плане заказчика её нет (К-2); толщины стен 300 / 120 мм приняты по плану заказчика, не замерены (К-1); разрешённая мощность 15 кВт принята по типовым ТУ для квартиры, ТУ заказчиком не переданы (К-4); подрайон климата не задан — принят не северный (жилые от 2,5 м) (К-9).
См. лист открытых вопросов (лист 6, записи К-1, К-2, К-4; лист 7, запись К-9).

1000 мм · печать 1:1

Изм.	Кол.уч	Лист	№ док.	Подп.	Дата
Разраб.		Кырлан А.С.			14.11.26
Пров.					
ГИП					
Н. контр.					
Утв.					

ГД-2026-007-АИ

Квартира 65 м²

Общая площадь 65,24* м² · * размеры со скана, не замерены (реестр — л. 6–8, К-1)

Дизайн-проект интерьера

Стадия	Лист	Листов
РП	69	117

Шкаф-купе М11

М 1:20

Кырлан Александр Сергеевич


выпуск 14.11.2026 № 9cc0b98f36 · стр. 77 из 139

Система хранения Г2


Кладовая (пом. 8) · вид из помещения · размеры в мм, отметки в м

ПРЕДВАРИТЕЛЬНО · не для производства работ · открыто пунктов: 14 (реестр — л. 6–8)


Общий вид (М 1:20)

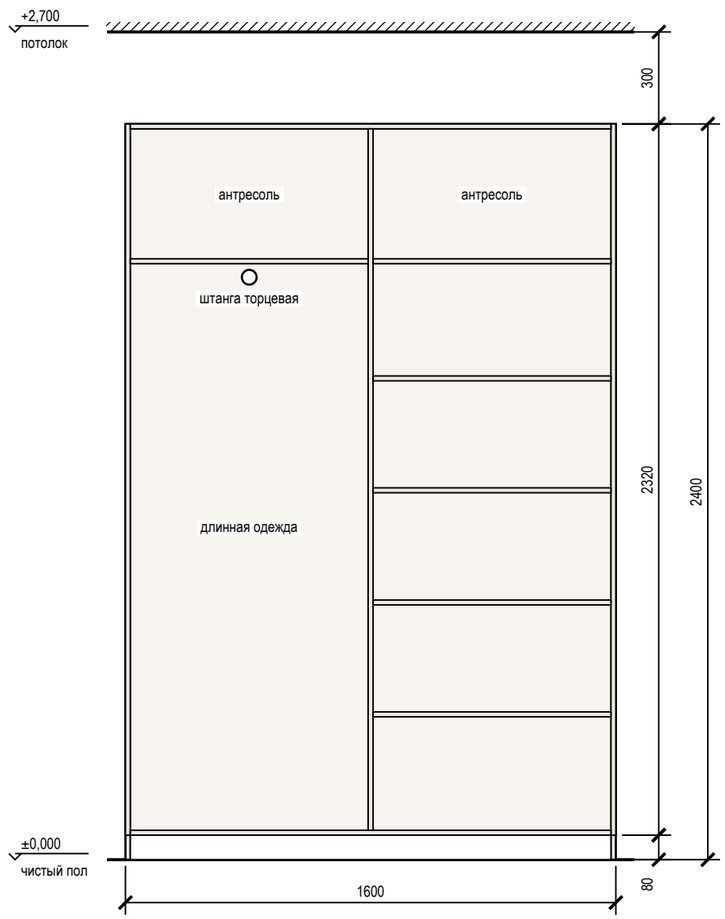


Наполнение, размеры в свету (М 1:20)

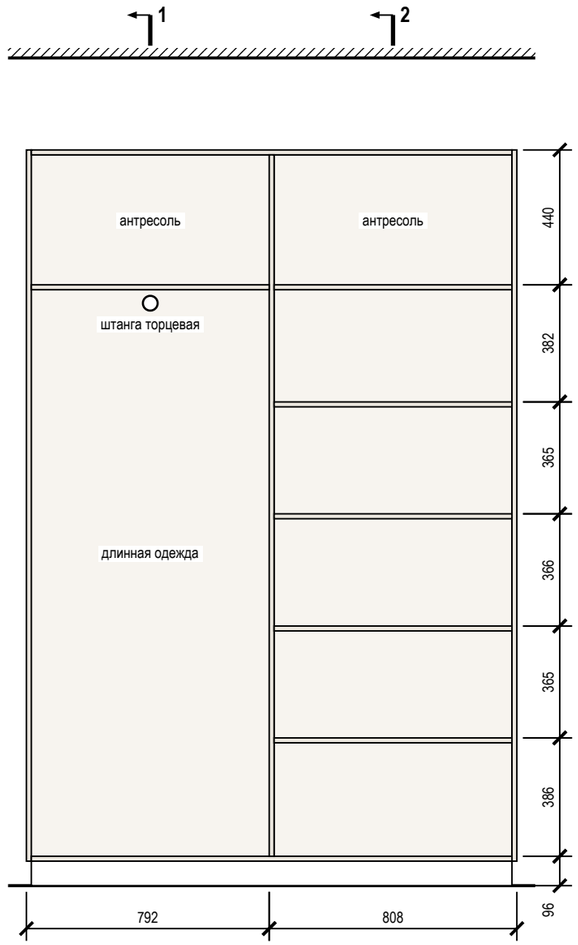

Разрез 1-1 (М 1:20)

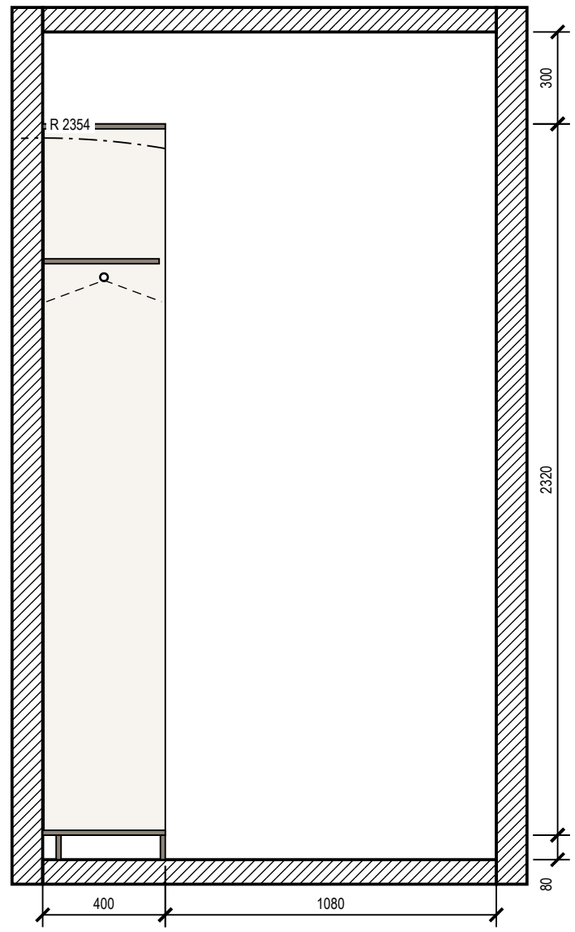

Разрез 2-2 (М 1:20)

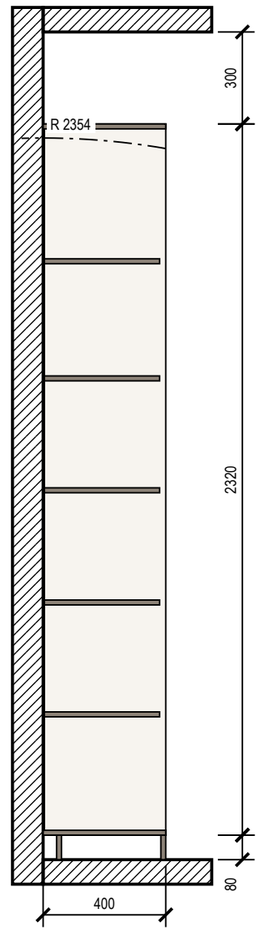

Примечания

1. Размеры — в мм по чистовой отделке; изделие 1600×400×2400 (Ш×Г×В). Перед раскроем — контрольный замер цеха после чистовой отделки стен, пола и потолка.
2. Корпус — ЛДСП 16 мм, задняя стенка ХДФ 4 мм в паз, цоколь 80 мм на регулируемых опорах; открытая система: без фасадов.
3. Кромка: скрытые торцы 0,4 мм, видимые 2 мм (ПВХ/АБС).
4. Присадка по 32-й системе — выполняет цех.
5. Зазор до потолка 300 мм.
6. Подъём корпуса: диагональ боковины без цоколя $\sqrt{(2320^2 + 400^2)} = 2354$ мм < 2700 мм до потолка — корпус собирается лёжа, поднимается поворотом и ставится на цоколь.
7. Крепление к стене от опрокидывания — уголки 2 шт. к несущему основанию (монтажная схема шкафов).
8. Проход перед изделием 1080 мм показан на разрезе 1-1.

Условные обозначения

- корпус и полки ЛДСП (вид на стену)
- задняя стенка ХДФ
- деталь в разрезе
- штанга для плечиков (на разрезе — плечики 450 мм)
- траектория угла корпуса при подъёме в проектное положение

Допущения и предложения на листе

Основа листа: размеры сняты с растрового плана заказчика без размеров: масштаб восстановлен по площадям помещений (≈ 11,8 мм на пиксель), контрольный обмер не выполнен (К-1); высота потолка 2700 мм принята: на плане заказчика её нет (К-2); толщины стен 300 / 120 мм приняты по плану заказчика, не замерены (К-1); разрешённая мощность 15 кВт принята по типовым ТУ для квартиры, ТУ заказчиком не переданы (К-4); подрайон климата не задан — принят не северный (жилые от 2,5 м) (К-9).
См. лист открытых вопросов (лист 6, записи К-1, К-2, К-4; лист 7, запись К-9).

1000 мм · печать 1:1

Изм.	Кол.уч	Лист	№ док.	Подп.	Дата
Разраб.		Кырлан А.С.			14.11.26
Пров.					
ГИП					
Н. контр.					
Утв.					

ГД-2026-007-АИ

Квартира 65 м²

Общая площадь 65,24* м² · * размеры со скана, не замерены (реестр — л. 6–8, К-1)

Дизайн-проект интерьера

Стадия	Лист	Листов
РП	70	117

Система хранения Г2

М 1:20

Кырлан Александр Сергеевич


выпуск 14.11.2026 № 9cc0b98f36 · стр. 78 из 139

Шкаф распашной С5


Детская (пом. 9) · вид из помещения · размеры в мм, отметки в м

ПРЕДВАРИТЕЛЬНО · не для производства работ · открыто пунктов: 14 (реестр — л. 6–8)


Вид с фасадами (М 1:25)

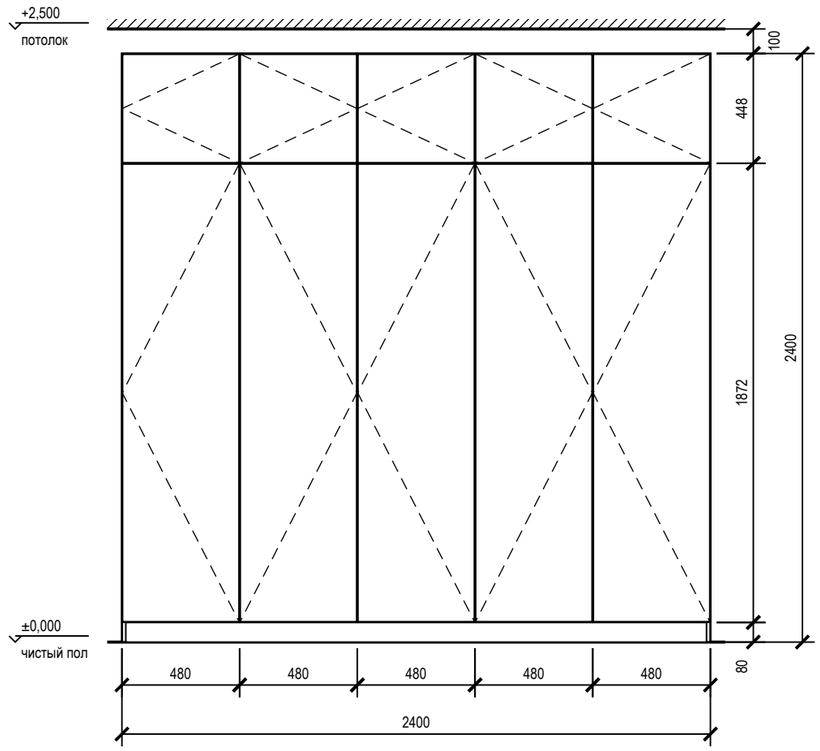


Вид без фасадов (М 1:25)

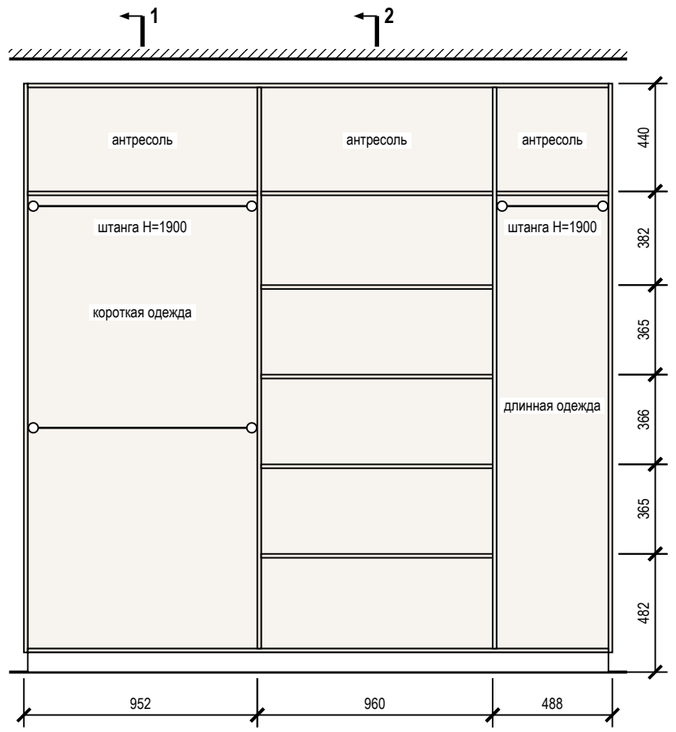

Разрез 1-1 (М 1:25)

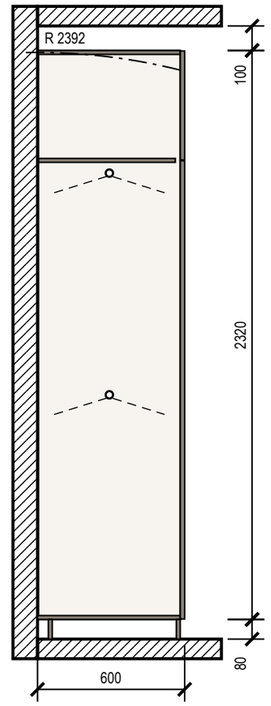

Разрез 2-2 (М 1:25)

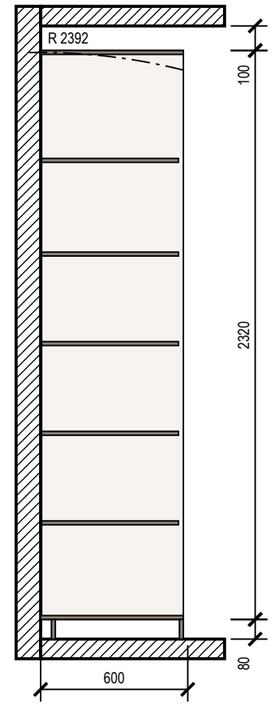

Примечания

1. Размеры — в мм по чистовой отделке; изделие 2400×600×2400 (Ш×Г×В). Перед раскроем — контрольный замер цеха после чистовой отделки стен, пола и потолка.
2. Корпус — ЛДСП 16 мм, задняя стенка ХДФ 4 мм в паз, цоколь 80 мм на регулируемых опорах; фасады накладные — МДФ 18 мм, эмаль матовая, 18 мм; цвет — по колерной карте; петли с доводчиком: фасад 1869 мм — 4 петли, фасад 445 мм — 2 петли.
3. Кромка: скрытые торцы 0,4 мм, видимые 2 мм (ПВХ/АБС).
4. Номинальные зазоры: между фасадами 3 мм, фасад — стена и фасад — потолок не менее 3 мм, фасад ящика — стойка 2 мм.
5. Присадка по 32-й системе — выполняет цех.
6. Зазор до потолка 100 мм — закрыть планкой в цвет корпуса при монтаже.
7. Подъём корпуса: диагональ боковины без цоколя √(2320² + 582²) = 2392 мм < 2500 мм до потолка — корпус собирается лёжа, поднимается поворотом и ставится на цоколь.
8. Крепление к стене от опрокидывания — уголки 2 шт. к несущему основанию (монтажная схема шкафов).

Условные обозначения

- фасад распашной: линии сходятся к стороне петель
- корпус и полки ЛДСП (вид на стену)
- задняя стенка ХДФ
- деталь в разрезе
- штанга для плечиков (на разрезе — плечики 450 мм)
- траектория угла корпуса при подъёме в проектное положение

Допущения и предложения на листе

Основа листа: размеры сняты с растрового плана заказчика без размеров: масштаб восстановлен по площадям помещений (≈ 11,8 мм на пиксель), контрольный обмер не выполнен (К-1); высота потолка 2700 мм принята: на плане заказчика её нет (К-2); толщины стен 300 / 120 мм приняты по плану заказчика, не замерены (К-1); разрешённая мощность 15 кВт принята по типовым ТУ для квартиры, ТУ заказчиком не переданы (К-4); подрайон климата не задан — принят не северный (жилые от 2,5 м) (К-9).
См. лист открытых вопросов (лист 6, записи К-1, К-2, К-4; лист 7, запись К-9).

1000 мм · печать 1:1

Изм.	Кол.уч	Лист	№ док.	Подп.	Дата
Разраб.		Кырлан А.С.			14.11.26
Пров.					
ГИП					
Н. контр.					
Утв.					

ГД-2026-007-АИ

Квартира 65 м²

Общая площадь 65,24* м² · * размеры со скана, не замерены (реестр — л. 6–8, К-1)

Дизайн-проект интерьера

Стадия	Лист	Листов
РП	71	117

Шкаф распашной С5

М 1:25

Кырлан Александр Сергеевич


выпуск 14.11.2026 № 9cc0b98f36 · стр. 79 из 139

Кухня (пом. 3). Развёртка гарнитура

Кухня-гостиная (пом. 3) · стена В · вид из помещения · размеры в мм, отметки в м · лист 1: вид с фасадами

ПРЕДВАРИТЕЛЬНО · не для производства работ · открыто пунктов: 14 (реестр — л. 6–8)

Вид с фасадами (М 1:20)

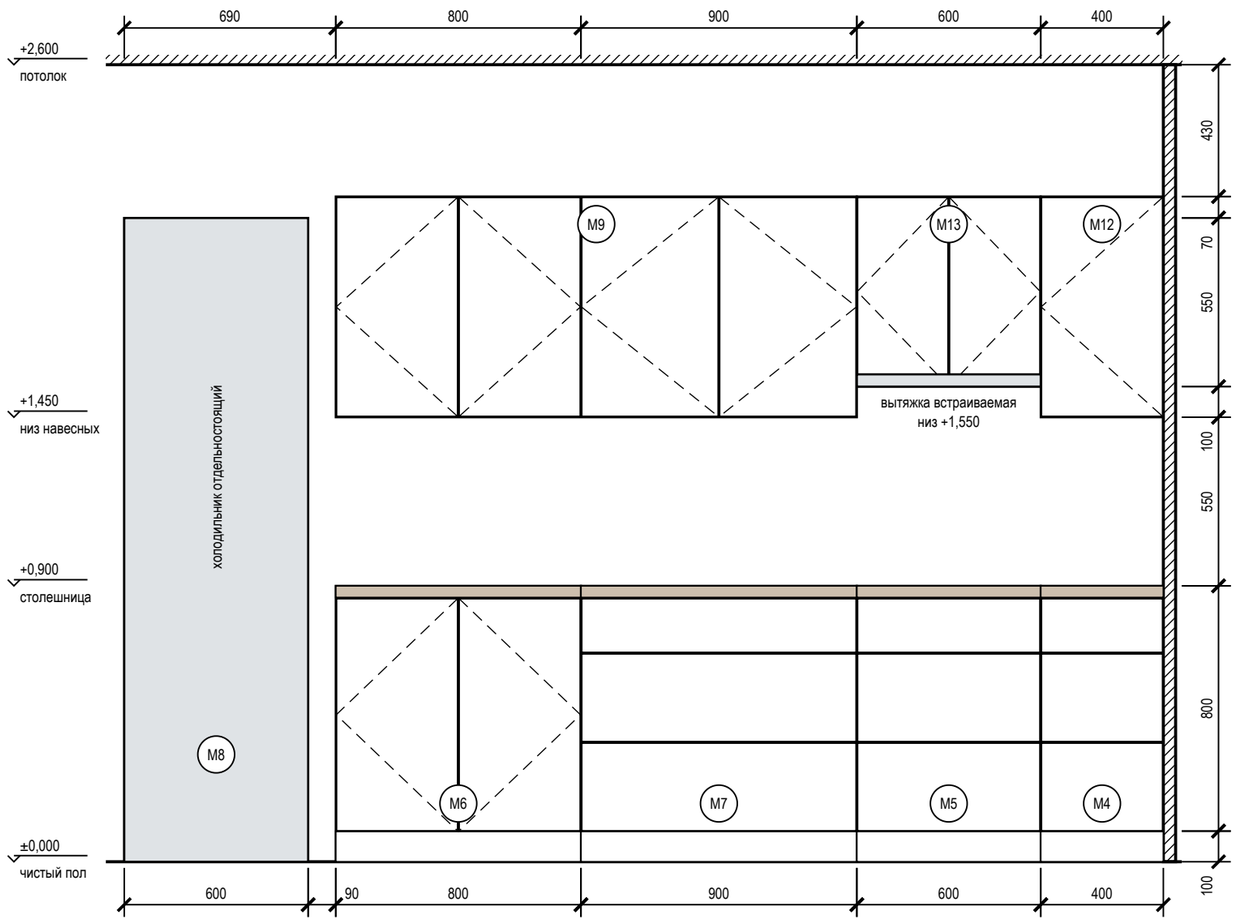

Условные обозначения

- фасад распашной: линии сходятся к стороне петель
- фасад ящика, карго
- встраиваемая техника
- столешница
- доборная планка
- деталь в разрезе
- K1 — марка изделия или модуля (на схеме расположения под ней — лист изделия)
- розетка на стене
- вывод кабеля к технике
- B1 — вывод воды В1 / Т3, канализации К1

Примечания

1. Размеры — в мм по чистовой отделке, вид из помещения; марки — как на плане расстановки. Перед раскроем — контрольный замер цеха после фартука и пола.
2. Корпуса — ЛДСП 16 мм, задняя стенка ХДФ 4 мм; фасады — МДФ эмаль 18 мм, цвет по колерной карте; столешница 38 мм, свес 20 мм; цоколь 100 мм.
3. Кромка: скрытые торцы 0,4 мм, видимые 1 мм. Номинальные зазоры: между фасадами 3 мм, фасад — столешница 3 мм, фасад — стена не менее 3 мм.
4. Ящики полного выдвижения и петли — с доводчиком; присадка по 32-й системе — выполняет цех.

Ведомость модулей

Мод.	Наименование	Ш×Г×В, мм	Низ, мм
M6	Модуль нижний: мойка	800×600×900	от цоколя
M7	Модуль нижний: ящики	900×600×900	от цоколя
M5	Модуль нижний: ящики, варочная	600×600×900	от цоколя
M4	Модуль нижний: ящики	400×600×900	от цоколя

Мод.	Наименование	Ш×Г×В, мм	Низ, мм
M9	Модуль навесной: сушка, полки	1700×350×720	+1450
M13	Модуль навесной: полки	600×350×620	+1550
M12	Модуль навесной: полки	400×350×720	+1450
M8	Место под холодильник отдельностоящий: без корпуса и фасада	600×650×2100	от пола

Допущения и предложения на листе

Основа листа: размеры сняты с растрового плана заказчика без размеров: масштаб восстановлен по площадям помещений (≈ 11,8 мм на пиксель), контрольный обмер не выполнен (К-1); высота потолка 2700 мм принята: на плане заказчика её нет (К-2); толщины стен 300 / 120 мм приняты по плану заказчика, не замерены (К-1); разрешённая мощность 15 кВт принята по типовым ТУ для квартиры, ТУ заказчиком не переданы (К-4); подрайон климата не задан — принят не северный (жилые от 2,5 м) (К-9).

См. лист открытых вопросов (лист 6, записи К-1, К-2, К-4; лист 7, запись К-9).

1000 мм · печать 1:1

Изм.	Кол.уч	Лист	№ док.	Подп.	Дата
Разраб.		Кырлан А.С.			14.11.26
Пров.					
ГИП					
Н. контр.					
Утв.					

ГД-2026-007-АИ

Квартира 65 м²

Общая площадь 65,24* м² · * размеры со скана, не замерены (реестр — л. 6–8, К-1)

Дизайн-проект интерьера

Стадия	Лист	Листов
РП	72	117

Кухня (пом. 3). Развёртка гарнитура

М 1:20

Кырлан Александр Сергеевич


выпуск 14.11.2026 № 9cc0b98f36 · стр. 80 из 139

Кухня (пом. 3). Развёртка гарнитура: вид без фасадов и разрезы


Кухня-гостиная (пом. 3) · стена В · вид из помещения · размеры в мм, отметки в м · лист 2: вид без фасадов, разрезы

ПРЕДВАРИТЕЛЬНО · не для производства работ · открыто пунктов: 14 (реестр — л. 6–8)


Вид без фасадов: наполнение, выводы (М 1:20)

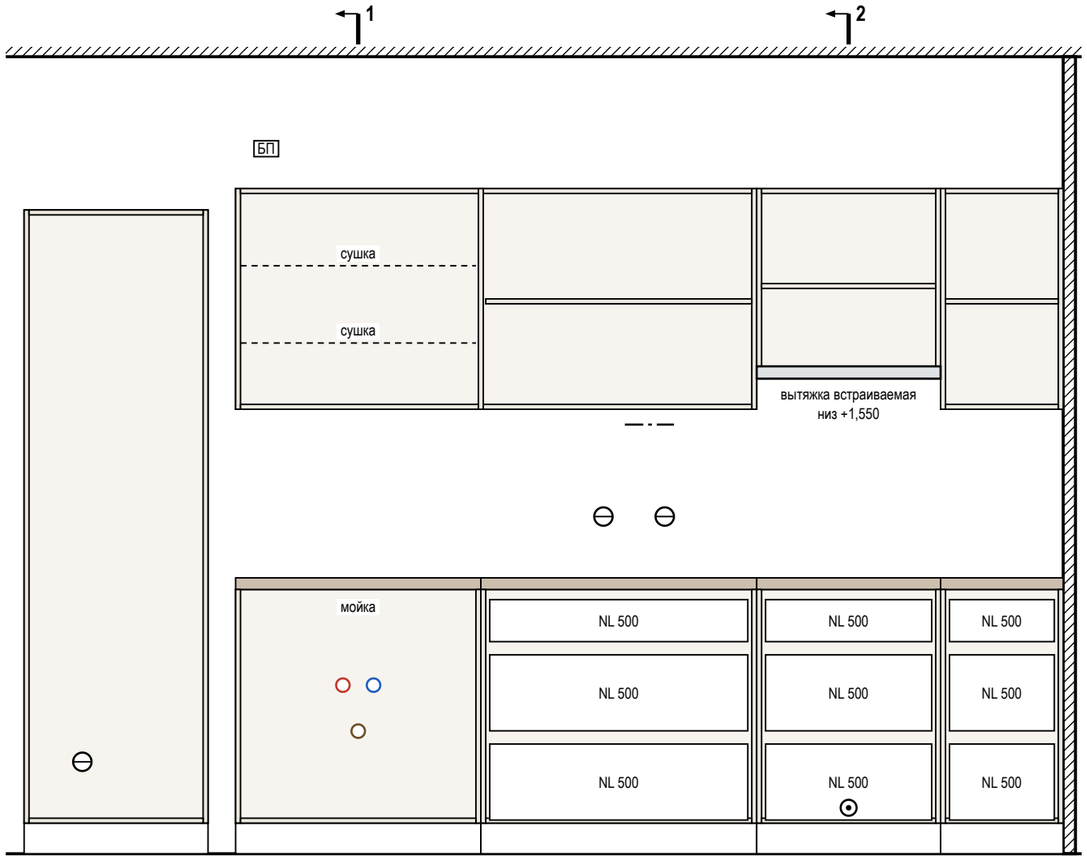

Разрез 1-1 (М 1:20)

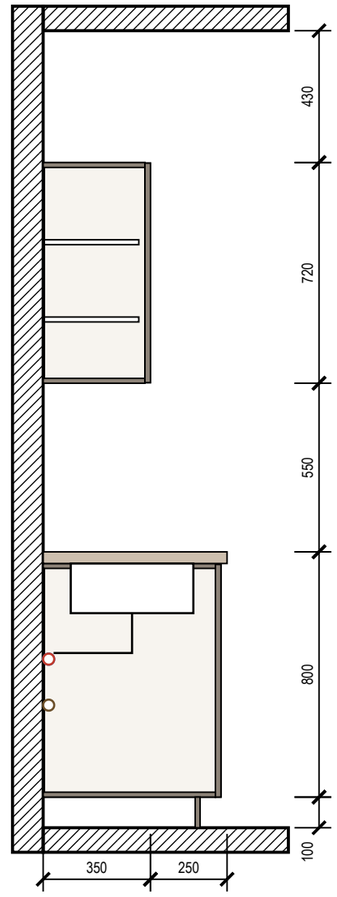

Разрез 2-2 (М 1:20)

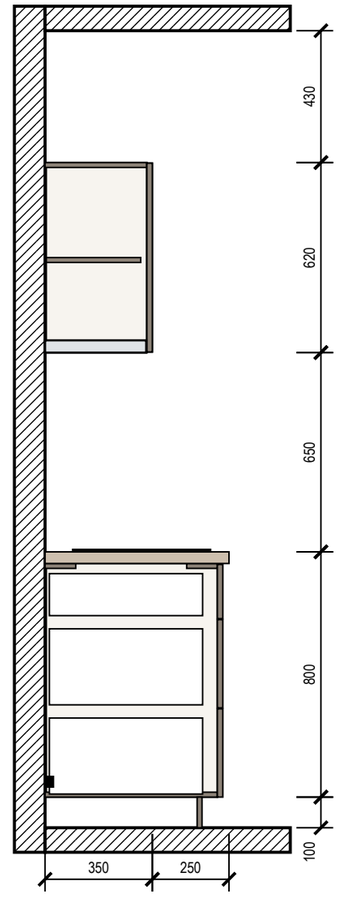

Примечания

1. Вытяжка встраивается в дно навесного модуля М13 над варочной: её низ на 1550 мм от пола, 650 мм над панелью (не меньше 650 мм).
2. Ниши техники — по монтажным схемам выбранных моделей: решётка в цоколе и канал за пеналом холодильника, зазор за духовым шкафом, фасад ПММ на двери машины.

Допущения и предложения на листе

Основа листа: размеры сняты с растрового плана заказчика без размеров: масштаб восстановлен по площадям помещений (≈ 11,8 мм на пиксель), контрольный обмер не выполнен (К-1); высота потолка 2700 мм принята: на плане заказчика её нет (К-2); толщины стен 300 / 120 мм приняты по плану заказчика, не замерены (К-1); разрешённая мощность 15 кВт принята по типовым ТУ для квартиры, ТУ заказчиком не переданы (К-4); подрайон климата не задан — принят не северный (жилые от 2,5 м) (К-9).
См. лист открытых вопросов (лист 6, записи К-1, К-2, К-4; лист 7, запись К-9).

1000 мм · печать 1:1

Изм.	Кол.уч	Лист	№ док.	Подп.	Дата
Разраб.		Кырлан А.С.			14.11.26
Пров.					
ГИП					
Н. контр.					
Утв.					

ГД-2026-007-АИ

Квартира 65 м²

Общая площадь 65,24* м² · * размеры со скана, не замерены (реестр — л. 6–8, К-1)

Дизайн-проект интерьера

Стадия	Лист	Листов
РП	73	117

Кухня (пом. 3). Развёртка гарнитура: вид без фасадов и разрезы
М 1:20

Кырлан Александр Сергеевич


выпуск 14.11.2026 № 9cc0b98f36 · стр. 81 из 139

Кухня (пом. 3). Монтажная схема


Кухня-гостиная (пом. 3) · стена В · размеры в мм от чистых поверхностей, высоты — от чистого пола

ПРЕДВАРИТЕЛЬНО · не для производства работ · открыто пунктов: 14 (реестр — л. 6–8)

Привязка выводов и крепление модулей (М 1:20)

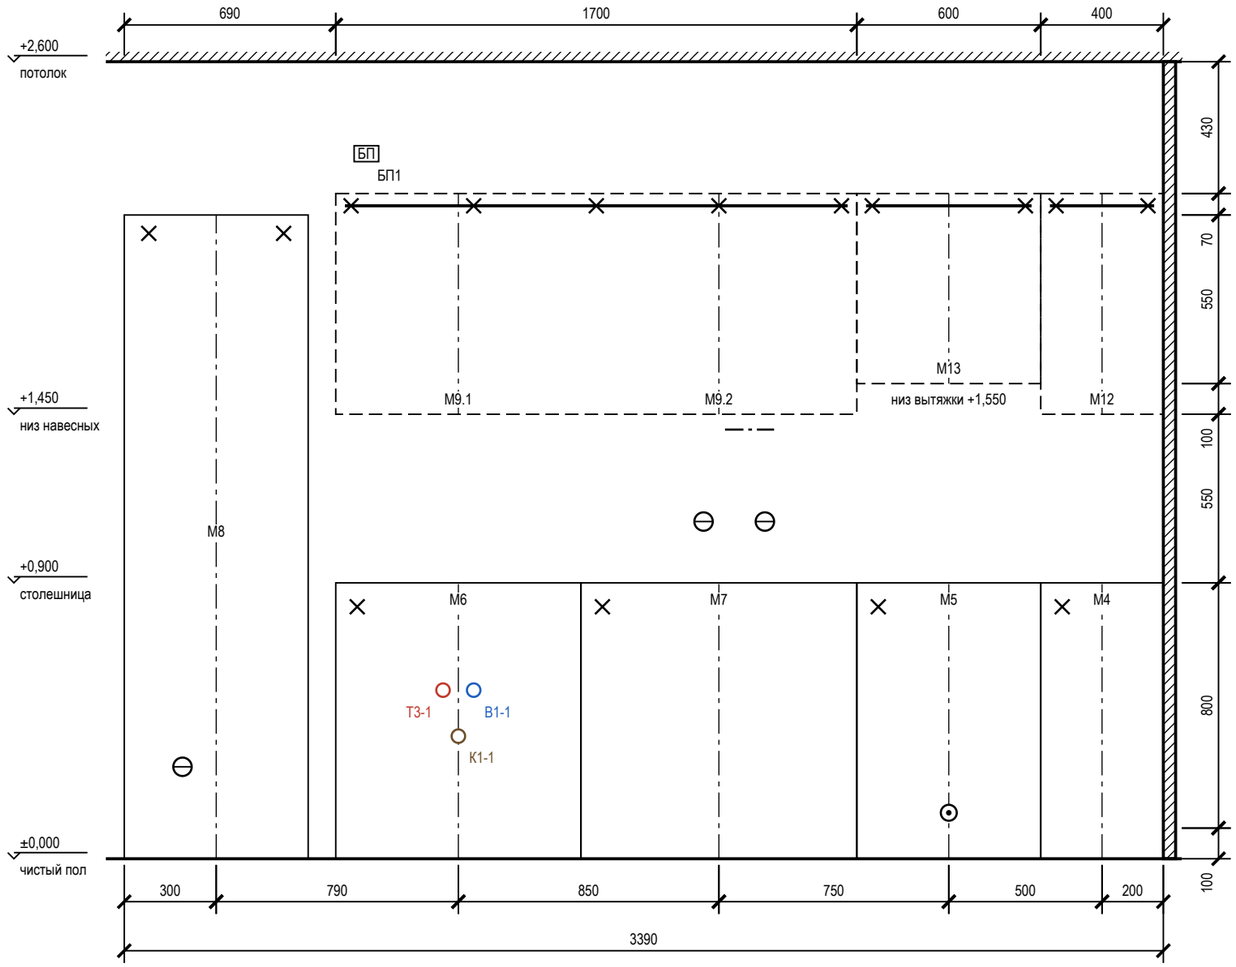

План столешницы (М 1:20)

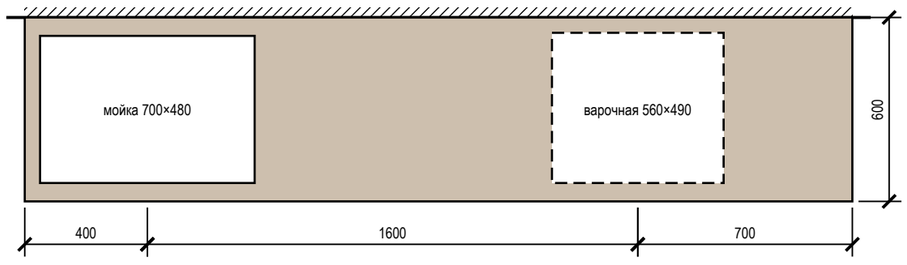

Привязка выводов к осям модулей

Код	Назначение	Модуль	От оси, мм	Н, мм	Размещение
	розетка — холодильник	М8	−110	300	за пеналом
БП1	блок питания	М9.1	−300	2300	в навесном модуле
Т3-1	Т3** — межос. 100	М6	−50	550	в модуле мойки
К1-1	К1 Ø50 — мойка	М6	0	400	в модуле мойки
В1-1	В1 — межос. 100	М6	+50	550	в модуле мойки
	розетка — рабочая зона	М7	−50	1100	над столешницей (фартук)
	светодиодная лента — подсветка столешницы	М7	+100	1400	в профиле по низу навесного модуля
	розетка ×2 — рабочая зона	М7	+150	1100	над столешницей (фартук)
	вывод кабеля — варочная панель	М5	0	150	в соседнем модуле, за ящиком

Зазоры под отделку

Поверхность	Отделка	Зазор, мм	Учесть
фартук	плитка / стеновая панель	10	от чернового основания до корпуса навесных и столешницы
стены	окраска	5	под штукатурку и шпаклёвку за пеналом
пол	инженерная доска		цоколь — после укладки пола, опоры ±20 мм

Условные обозначения

- нижний модуль, пенал (контур)
- невидимый контур: навесной модуль, корпус под столешницей
- ось модуля (от неё — привязка вывода)
- анкер / уголок крепления к стене
- розетка на стене
- вывод кабеля к технике
- В1 — вывод воды В1 / Т3, канализации К1

Допущения и предложения на листе

Основа листа: размеры сняты с растрового плана заказчика без размеров: масштаб восстановлен по площадям помещений (≈ 11,8 мм на пиксель), контрольный обмер не выполнен (К-1); высота потолка 2700 мм принята: на плане заказчика её нет (К-2); толщины стен 300 / 120 мм приняты по плану заказчика, не замерены (К-1); разрешённая мощность 15 кВт принята по типовым ТУ для квартиры, ТУ заказчиком не переданы (К-4); подрайон климата не задан — принят не северный (жилые от 2,5 м) (К-9).
Знак «**» — предложение проектировщика, заказчиком не утверждено (согласовать с заказчиком): ИЗ-4: Т3.
См. лист открытых вопросов (лист 6, записи К-1, К-2, К-4; лист 7, запись К-9; лист 8, запись ИЗ-4).

Примечания

1. Выводы — по проекту электрики и ВК; привязка по горизонтали — от оси модуля (плюс — вправо по виду), по высоте — от чистого пола до оси вывода.
2. Пенал — уголки к стене 2 шт. сверху; нижние модули — стяжками между собой и уголком к стене; ряд выставить по уровню опорами цоколя.
3. Розетки над столешницей — не ниже 150 мм над ней и не за корпусом техники; розетка за ПММ, духовым шкафом и холодильником — только в соседнем модуле или в зоне цоколя с доступом.
4. Столешница — вырезы по шаблонам выбранных моделей мойки и варочной панели; торцы у стены — герметик, пристеночный плинтус.

1000 мм · печать 1:1

Изм.	Кол.уч	Лист	№ док.	Подп.	Дата
Разраб.		Кырлан А.С.			14.11.26
Пров.					
ГИП					
Н. контр.					
Утв.					

ГД-2026-007-АИ

Квартира 65 м²

Общая площадь 65,24* м² · * размеры со скана, не замерены (реестр — л. 6–8, К-1)

Дизайн-проект интерьера

Стадия	Лист	Листов
РП	74	117

Кухня (пом. 3). Монтажная схема

М 1:20

Кырлан Александр Сергеевич


выпуск 14.11.2026 № 9cc0b98f36 · стр. 82 из 139

Кухня (пом. 3). Столешница: план

Кухня-гостиная (пом. 3) · размеры в мм · вид сверху

План столешницы (вид сверху, стена вверху) М 1:20

Ст-1: стена С, 2700×600

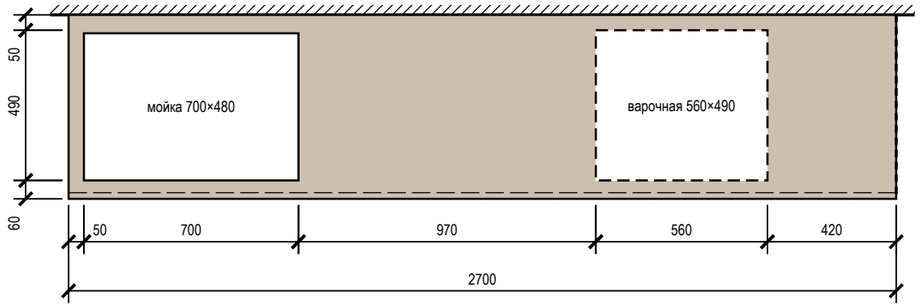

свес над фасадами 20 мм · толщина 38 мм*

Ведомость столешниц

Марка	Стена	Д×Ш×Т, мм	Материал	Вырезы	Кромка	Стыки
Ст-1	С	2700×600×38*	материал не задан (materials.worktop.mat	мойка 700×480; варочная 560×490	3,30 пог. м	нет
Итого			**S = 1,62 м²**		**3,30 пог. м**	

Примечания

1. Материал: материал не задан (materials.worktop.mat) (materials.worktop.mat в данных не задан); толщина 38 мм*.
2. * — толщина принята по практике (38 мм): в данных изделия materials.worktop.thk не задана.
3. Розеток в столешнице нет: питание над столешницей — на фартуке (план розеток), не за корпусом техники.
4. Вырезы: мойка — по габариту чаши 700×480 (прибор), отступ от стены 60 мм; варочная панель — ориентир 560×490 мм, отступ от стены 50 мм; вырезы разметить по шаблону выбранных моделей, углы выреза — радиус не менее 5 мм.
5. Радиусы углов и фаска кромки в данных не заданы: углы столешницы прямые, кромка — прямая без фаски, пока не задано иное.
6. Стыков нет: каждая столешница — одной деталью.
7. Свес над фасадами — 20 мм; торцы: свободный торец — кромка, торец у стены или пенала — зазор не более 3 мм, герметик. Длина кромки — по лицевой стороне и свободным торцам.

Допущения и предложения на листе

Основа листа: размеры сняты с растрового плана заказчика без размеров: масштаб восстановлен по площадям помещений (≈ 11,8 мм на пиксель), контрольный обмер не выполнен (К-1); высота потолка 2700 мм принята: на плане заказчика её нет (К-2); толщины стен 300 / 120 мм приняты по плану заказчика, не замерены (К-1); разрешённая мощность 15 кВт принята по типовым ТУ для квартиры, ТУ заказчиком не переданы (К-4); подрайон климата не задан — принят не северный (жилые от 2,5 м) (К-9).
См. лист открытых вопросов (лист 6, записи К-1, К-2, К-4; лист 7, запись К-9).

1000 мм · печать 1:1

Изм.	Кол.уч	Лист	№ док.	Подп.	Дата
Разраб.		Кырлан А.С.			14.11.26
Пров.					
ГИП					
Н. контр.					
Утв.					

ГД-2026-007-АИ

Квартира 65 м²

Общая площадь 65,24* м² · * размеры со скана, не замерены (реестр — л. 6–8, К-1)

Дизайн-проект интерьера

Стадия	Лист	Листов
РП	75	117

Кухня (пом. 3). Столешница: план

М 1:20

Кырлан Александр Сергеевич


выпуск 14.11.2026 № 9cc0b98f36 · стр. 83 из 139

Шкафы. Монтажная схема


крепление к стене, установочные размеры, зазоры под отделку · размеры в мм

ПРЕДВАРИТЕЛЬНО · не для производства работ · открыто пунктов: 14 (реестр — л. 6–8)


Система хранения Г1 (пом. 1) (М 1:40)

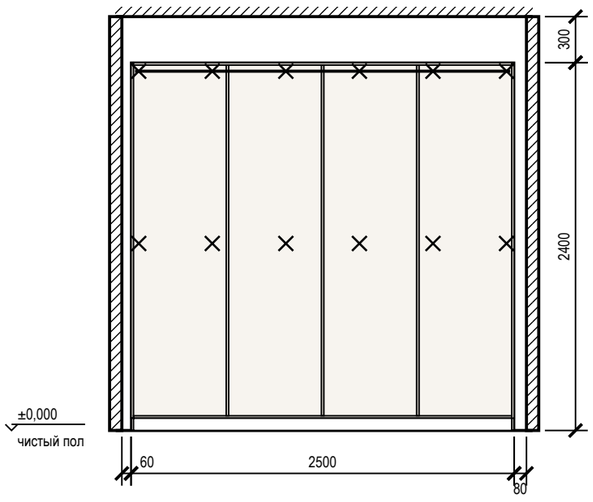


Шкаф-купе М11 (пом. 4) (М 1:40)

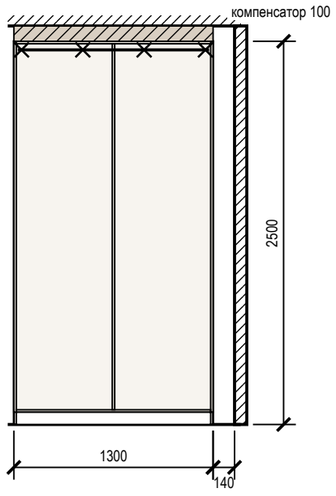

Система хранения Г2 (пом. 8) (М 1:40)

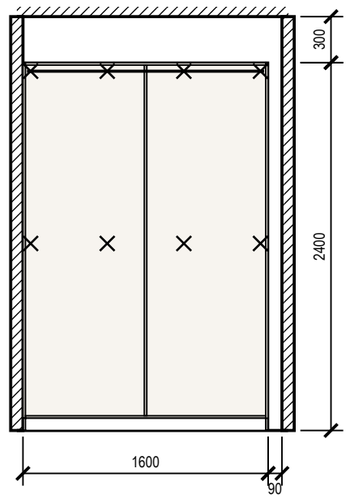

Шкаф распашной С5 (пом. 9) (М 1:40)

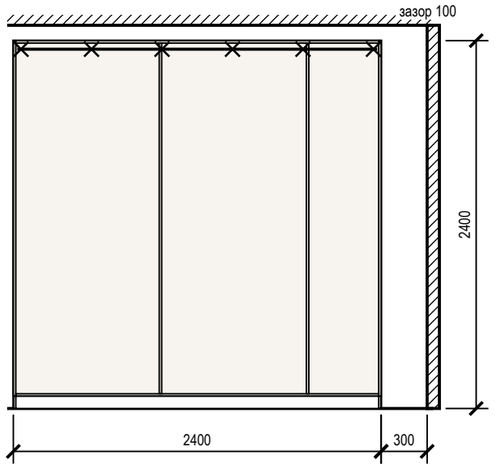

Крепление и зазоры под отделку

Марка	Помещение, стена	Основание	Отделка стены	Зазор, мм	Крепёж по планке	От опрокидывания
Г1	Гардеробная (1), стена А	по основанию — см. таблицу крепежа	окраска	5	анкер 12 шт. (2 ряда)	крепление к стене, 3 точки
М11	Прихожая (4), стена Б	по основанию — см. таблицу крепежа	окраска	5	анкер 4 шт., шаг 400	уголки 2 шт.
Г2	Кладовая (8), стена Б	по основанию — см. таблицу крепежа	окраска	5	анкер 8 шт. (2 ряда)	уголки 2 шт.
С5	Детская (9), стена А	по основанию — см. таблицу крепежа	окраска	5	анкер 6 шт., шаг 460	уголки 2 шт.

Крепёж по основанию стены

Основание стены	Крепёж
бетон, ж/б	анкер-шуруп 7,5×72 или дюбель 8×60 с шурупом 5×70
кирпич полнотелый	дюбель 8×80 с шурупом 5×90
газобетон, пазогребень	дюбель для газобетона 10×100 или химический анкер
гипсокартон	закладная до обшивки (брус 40×80 или фанера 18 мм), саморез в закладную

Условные обозначения

- анкер / уголок крепления к стене
- корпус и полки ЛДСП (вид на стену)
- компенсатор — короб до потолка

Примечания

1. Установочные размеры — от чистого пола и чистых стен; перед установкой контрольный замер после отделки.
2. Порядок: корпус выставить по уровню опорами цоколя → закрепить к стене по задней планке → навесить двери и фасады, отрегулировать зазоры → подогнать и закрепить компенсатор.
3. Анкеры — с шагом не более 500 мм, не ближе 50 мм от края планки; на ГКЛ только в закладную, установленную до обшивки.
4. Скрытые коммуникации под анкеры проверить детектором; трассы электрики по плану розеток.

Допущения и предложения на листе

Основа листа: размеры сняты с растрового плана заказчика без размеров: масштаб восстановлен по площадям помещений (≈ 11,8 мм на пиксель), контрольный обмер не выполнен (К-1); высота потолка 2700 мм принята: на плане заказчика её нет (К-2); толщины стен 300 / 120 мм приняты по плану заказчика, не замерены (К-1); разрешённая мощность 15 кВт принята по типовым ТУ для квартиры, ТУ заказчиком не переданы (К-4); подрайон климата не задан — принят не северный (жилые от 2,5 м) (К-9).
См. лист открытых вопросов (лист 6, записи К-1, К-2, К-4; лист 7, запись К-9).

1000 мм · печать 1:1

Изм.	Кол.уч	Лист	№ док.	Подп.	Дата
Разраб.		Кырлан А.С.			14.11.26
Пров.					
ГИП					
Н. контр.					
Утв.					

ГД-2026-007-АИ

Квартира 65 м²

Общая площадь 65,24* м² · * размеры со скана, не замерены (реестр — л. 6–8, К-1)

Дизайн-проект интерьера

Стадия	Лист	Листов
РП	76	117

Шкафы. Монтажная схема

М 1:40

Кырлан Александр Сергеевич

выпуск 14.11.2026 № 9cc0b98f36 · стр. 84 из 139

Ведомости изделий, техники и фурнитуры

встроенная мебель и кухонный гарнитур · размеры в мм

Ведомость изделий

Марка	Наименование	Пом.	Ш×Г×В, мм	Корпус	Фасад	Кромка, мм	Кол.
Г1	Система хранения	1	2500×600×2400	ЛДСП 16	без фасадов	0,4 / 2 *	1
М11	Шкаф-купе	4	1300×600×2500	ЛДСП 16	ЛДСП 10 мм в алюминиевом профиле	0,4 / 1	1
Г2	Система хранения	8	1600×400×2400	ЛДСП 16	без фасадов	0,4 / 2 *	1
С5	Шкаф распашной	9	2400×600×2400	ЛДСП 16	МДФ 18 мм, эмаль матовая	0,4 / 2 *	1
М8	Место под холодильник отдельностоящий: без корпуса и фасада	3	600×650×2100 (место в ряду)	без корпуса	без фасада (прибор отдельностоящий)		
М6	Модуль нижний: мойка	3	800×600×900	ЛДСП 16	МДФ эмаль 18 мм	0,4 / 1	1
М9	Модуль навесной: сушка, полки	3	1700×350×720	ЛДСП 16	МДФ эмаль 18 мм	0,4 / 1	1
М7	Модуль нижний: ящики	3	900×600×900	ЛДСП 16	МДФ эмаль 18 мм	0,4 / 1	1
М5	Модуль нижний: ящики, варочная	3	600×600×900	ЛДСП 16	МДФ эмаль 18 мм	0,4 / 1	1
М13	Модуль навесной: полки	3	600×350×620	ЛДСП 16	МДФ эмаль 18 мм	0,4 / 1	1
М4	Модуль нижний: ящики	3	400×600×900	ЛДСП 16	МДФ эмаль 18 мм	0,4 / 1	1
М12	Модуль навесной: полки	3	400×350×720	ЛДСП 16	МДФ эмаль 18 мм	0,4 / 1	1

Ведомость встраиваемой техники

Поз.	Прибор	Ниша, вырез, мм	Вентиляция	Питание	Схема
М8	Холодильник отдельностоящий	проём 600, зазор сверху ≥ 50	по паспорту модели	М8, Н=300 — за пеналом	по модели
М6	Мойка врезная / подстольная с сифоном	вырез по шаблону, ориентир 700 × 480		смеситель — выводы ВК	по модели
М5	Варочная панель индукционная, 60 см	вырез в столешнице 560 × 490		М5, Н=150 — в соседнем модуле, за ящиком	по модели
М13	Вытяжка встраиваемая в навесной модуль, 60 см	низ ≥ 650 над панелью	воздуховод к вентканалу, короб до потолка	питание: точка ЭОМ не задана — вывод под прибор не делать до задания	по модели

Ведомость фурнитуры

№	Фурнитура	Тип, размер	Изделия	Кол.
1	Полкодержатель с фиксацией	ø5 мм	Г1, М11, Г2, С5, М9, М13, М12	140
2	Штанга овальная 30×15, L = 605	+ 2 держателя	Г1	2
3	Опора регулируемая с цоколем на клипсах	ход 20 мм	Г1, М11, Г2, С5	30
4	Анкер по основанию стены	по таблице крепежа	Г1, М11, Г2, С5, М9, М13, М12	39
5	Уголок крепления к стене от опрокидывания	стальной	Г1, М11, Г2, С5	8
6	Система дверей купе: профиль, направляющие, ролики	на 2 двери	М11	1
7	Ручка-профиль вертикальная	в цвет профиля	М11	2
8	Штанга овальная 30×15, L = 626	+ 2 держателя	М11	1
9	Полка для обуви выдвижная наклонная	ширина 626	М11	3
10	Штанга выдвижная торцевая	L по глубине	Г2	1
11	Петля накладная 110° с доводчиком	чашка 35 мм	С5, М6, М9, М13, М12	48
12	Штанга овальная 30×15, L = 936	+ 2 держателя	С5	2
13	Штанга овальная 30×15, L = 456	+ 2 держателя	С5	1
14	Ручка-профиль	латунь матовая	М6, М9, М7, М5, М13, М4, М12	18
15	Опора кухонная регулируемая 100–120 мм	+ клипса цоколя	М6, М7, М5, М4	20
16	Сушка для посуды в шкаф	ширина 800	М9	1
17	Навес регулируемый для навесного шкафа	пара на секцию	М9, М13, М12	4
18	Шина монтажная	L = 1640	М9	1
19	Направляющие полного выдвижения с доводчиком NL 500	пара	М7, М5, М4	9
20	Шина монтажная	L = 540	М13	1
21	Шина монтажная	L = 340	М12	1

Примечания

1. Модели техники выбирает заказчик до изготовления мебели; ниши, вырезы и вентиляция — по монтажной схеме выбранной модели (условие гарантии), её номер вносится в ведомость.
2. Количество фурнитуры — по чертежам изделий; запас крепежа 5 %. Аналоги — по характеристикам (доводчик, нагрузка, ход).
3. Цвет корпусов, фасадов и профилей — по колерной карте проекта. Кромка — скрытые / видимые торцы, мм.
4. * Кромка в данных изделия не задана: принята ПВХ 0,4 мм на скрытых торцах и 2 мм на видимых (по умолчанию для ЛДСП корпуса и МДФ фасада); заказчик или мебельщик подтверждает до раскроя.

Допущения и предложения на листе

Основа листа: размеры сняты с растрового плана заказчика без размеров: масштаб восстановлен по площадям помещений (≈ 11,8 мм на пиксель), контрольный обмер не выполнен (К-1); высота потолка 2700 мм принята: на плане заказчика её нет (К-2); толщины стен 300 / 120 мм приняты по плану заказчика, не замерены (К-1); разрешённая мощность 15 кВт принята по типовым ТУ для квартиры, ТУ заказчиком не переданы (К-4); подрайон климата не задан — принят не северный (жилые от 2,5 м) (К-9).
См. лист открытых вопросов (лист 6, записи К-1, К-2, К-4; лист 7, запись К-9).

Изм.	Кол.уч	Лист	№ док.	Подп.	Дата
Разраб.		Кырлан А.С.			14.11.26
Пров.					
ГИП					
Н. контр.					
Утв.					

ГД-2026-007-АИ

Квартира 65 м²

Общая площадь 65,24* м² · * размеры со скана, не замерены (реестр — л. 6–8, К-1)

Дизайн-проект интерьера

Стадия	Лист	Листов
РП	77	117

Ведомости изделий, техники и фурнитуры

М б/м

Кырлан Александр Сергеевич

выпуск 14.11.2026 № 9cc0b98f36 · стр. 85 из 139

ПРЕДВАРИТЕЛЬНО · не для производства работ · открыто пунктов: 14 (реестр — л. 6–8)

Сводка листовых материалов и кромки

ЛДСП, МДФ, ХДФ и кромка по изделиям · площади в м², кромка в пог. м

Листовые материалы по толщинам и декорам

Материал, декор	Назначение	Изделий	S, м²	S × 1,15*, м²
ЛДСП 16 мм*	корпус	4	39,91	45,90
ЛДСП 16 мм	корпус	7	9,79	11,26
ХДФ 4 мм	задняя стенка	11	22,17	25,49
МДФ 18 мм, эмаль матовая	фасад	1	5,52	6,34
МДФ эмаль 18 мм	фасад	7	3,89	4,47
ЛДСП 10 мм в алюминиевом профиле	фасад	1	3,05	3,50
Итого			**84,32**	**96,97**

Кромка по типам

Кромка	Толщина, мм	Длина, пог. м	+10 %*, пог. м
видимая (передний торец, торец фасада ЛДСП)	2	121,5	133,6
скрытая (задний торец деталей корпуса)	0,4	94,0	103,4

Примечания

1. Площади — по моделям изделий листов мебельщика: боковины, дно, крыша (у нижнего кухонного модуля — дно и две царги по 100 мм), полки, стойки, задняя стенка ХДФ, цоколь, фасады. Коэффициент раскроя 1,15* — обрезь, пропилы и подбор рисунка; сводка — для заказа материала, раскрой делает цех.
2. Кромка: видимая — передний торец деталей корпуса и периметр фасада из ЛДСП; скрытая — задний торец деталей корпуса. Фасады из МДФ (эмаль, шпон) кромки не имеют. Толщина — из materials.edge изделий; где не задана — по умолчанию 2 и 0,4 мм*.
3. Не вошло: короба ящиков (в комплекте направляющих NL), столешница (лист «Столешница: план» и раскрой камня), остров, встроенная техника, покупные изделия.
4. * — значение принято по практике, не задано в данных.

Изделия (11)

Изделие	Пом.	Корпус, м²	ХДФ, м²	Фасад, м²	Кромка, пог. м
Г1 Система хранения	1	14,24	5,80	0,00	49,9
М11 Шкаф-купе	4	8,05	3,15	3,05	41,5
Г2 Система хранения	8	5,90	3,71	0,00	31,0
С5 Шкаф распашной	9	11,72	5,57	5,52	42,5
М6 модуль кухни	3	1,52	0,61	0,60	6,9
М9 модуль кухни	3	2,34	1,22	1,21	14,4
М7 модуль кухни	3	1,61	0,69	0,68	7,4
М5 модуль кухни	3	1,35	0,46	0,45	5,9
М13 модуль кухни	3	0,97	0,37	0,37	5,9
М4 модуль кухни	3	1,18	0,30	0,30	4,9
М12 модуль кухни	3	0,84	0,29	0,28	5,1

Допущения и предложения на листе

Основа листа: размеры сняты с растрового плана заказчика без размеров: масштаб восстановлен по площадям помещений (≈ 11,8 мм на пиксель), контрольный обмер не выполнен (К-1); высота потолка 2700 мм принята: на плане заказчика её нет (К-2); толщины стен 300 / 120 мм приняты по плану заказчика, не замерены (К-1); разрешённая мощность 15 кВт принята по типовым ТУ для квартиры, ТУ заказчиком не переданы (К-4); подрайон климата не задан — принят не северный (жилые от 2,5 м) (К-9).
Знак «**» — предложение проектировщика, заказчиком не утверждено (согласовать с заказчиком): пол пом. 1–3, 8, 9 — артикул выбран из каталога: Coswick 1167-1101 (инженерная доска, дуб натуральный, лак, 2100×127 мм); предложение исполнителя — выбор подтверждает автор; цены в каталоге нет, в смете «по КП».
См. лист открытых вопросов (лист 6, записи К-1, К-2, К-4; лист 7, запись К-9).

Изм.	Кол.уч	Лист	№ док.	Подп.	Дата
Разраб.		Кырлан А.С.			14.11.26
Пров.					
ГИП					
Н. контр.					
Утв.					

ГД-2026-007-АИ

Квартира 65 м²

Общая площадь 65,24* м² · * размеры со скана, не замерены (реестр — л. 6–8, К-1)

Дизайн-проект интерьера

Стадия	Лист	Листов
РП	78	117

Сводка листовых материалов и кромки

М б/м

Кырлан Александр Сергеевич

09

Развёртки и узлы



Кырлан Александр Сергеевич

выпуск 14.11.2026 № 9cc0b98f36 · стр. 87 из 139

Реестр марок отделки и позиций альбома

Реестр марок отделки (О ↔ позиции колерной карты) и марки позиций по видам

Реестр марок отделки альбома

Марка	Поверхность	Материал, изделие	Цвет, код	Помещения	Колер. карта
О1	стены	окраска, Tikkurila Harmony, матовая, подготовка Q3	Tikkurila V503 «Winter»	1	К1
О2	плинтус	плинтус МДФ, Orac Decor Contour (Luxxus), h 69 мм, SX165	Tikkurila V503 «Winter»	1	К3
О3	потолок	окраска, Tikkurila Anti-Reflex 2, глубокоматовая, подготовка Q3	Tikkurila V503 «Winter»	1, 9	К2
О4	пол	инженерная доска, Coswick Классическая, 2100×127 мм, 1167-1101		1, 2, 3, 8, 9	КМ1
О5	стены	окраска, Tikkurila, глубокоматовая, подготовка Q3	NCS S 1502-Y50R	2, 4, 5	К4, К9
О6	плинтус	плинтус МДФ, Orac Decor Contour (Luxxus), h 69 мм, SX165, шелковисто-матовая	NCS S 0300-N	2, 3, 4, 5, 8	К6
О7	потолок	окраска, Tikkurila, глубокоматовая	NCS S 0300-N	2, 3, 4, 5, 6, 7, 8	К5, К8
О8	стены	окраска, Tikkurila, шелковисто-матовая, подготовка Q3	NCS S 1002-Y50R	3	К7
О9	пол	керамогранит, Kerama Marazzi Королевская дорога, 600×1200 мм, SG501600R	Kerama Marazzi SG501600R «Королевская дорога»	4, 5, 6, 7	КМ2
О10	стены	облицовка плиткой, Italon Charme Extra, 600×1200 мм, 610010001195	Italon 610010001195 «Charme Extra»	6, 7	КМ3
О11	стены	окраска, Tikkurila, матовая, подготовка Q3	NCS S 0502-Y	8	К10
О12	стены	окраска, Farrow & Ball Modern Emulsion, матовая, подготовка Q3	Farrow & Ball No. 241 «Skimming Stone»	9	К11
О13	акцентная стена	окраска, Farrow & Ball Modern Emulsion, матовая, подготовка Q3	Farrow & Ball No. 30 «Hague Blue»	9	К12
О14	плинтус	плинтус МДФ, Orac Decor Contour (Luxxus), h 69 мм, SX165	Farrow & Ball No. 241 «Skimming Stone»	9	К13

Марки позиций альбома по видам

Префикс	Что обозначает, позиции	Листы
Д	двери: Д-1–Д-5	21–23
ПР	проёмы без полотна (порталы): ПР-1	21–23
ОК	окна: ОК-1–ОК-4	21–23
Г, М, С	мебель и оборудование: Г1, Г2, М1**, М2**, М3**, М4–М13, С1–С8	24–28
П	сантехнические приборы: П1, П3–П5, П20–П22	39–47
ДК	декор (картины, зеркала, растения): ДК1**, ДК2**, ДК3, ДК4, ДК5**, ДК6**, ДК7**, ДК8**, ДК9**, ДК10**, ДК11**, ДК12**, ДК13**, ДК14**	1, 61–66
Т	текстиль (шторы, ковры): Т1**, Т2**, Т3**, Т4**, Т5**, Т6**, Т7–Т12, Т13**, Т14**, Т15**, Т16**, Т17**, Т18**, Т19**, Т20**	1, 61–66
Св	светильники: Св1–Св4, Св5**, Св6–Св26	29–36
Р	розетки: Р1–Р11, Р12**, Р13–Р21	29–36
S	выключатели: S1–S8	29–36

Марки позиций альбома по видам (продолжение)

Префикс	Что обозначает, позиции	Листы
ИП	извещатели: ИП1, ИП2, ИП3**, ИП4**, ИП5	29–36
LAN	розетки компьютерные: LAN1–LAN4	29–36
БП	блоки питания LED: БП1–БП3	29–36
ТВ	розетки ТВ: ТВ1, ТВ2	29–36
ЭВ	выводы кабеля: ЭВ1–ЭВ3	29–36
ЩК	щиты: ЩК	29–36
ДФ	домофон: ДФ1	29–36
КУП	электроустановочные изделия: КУП1	29–36
Ст В1, Ст К1, Ст Т3**	стояки (системы В1, Т3**, К1): Ст В1-1, Ст К1-1, Ст Т3-1	39–47
О	марки отделки (реестр альбома): О1–О14	2–5, 79–103
К, КМ	позиции колерной карты: К1–К13, КМ1–КМ3	58–60
Р	радиаторы отопления: Р-1–Р-4	37, 38

Примечания

1. Марка отделки О — одна на весь альбом: одна и та же отделка (материал, изделие, цвет, формат) на всех листах имеет одну марку; на развёртках и планах стоят марки этого реестра.
2. Столбец «Колер. карта» — позиции колерной карты (лист 58): К — окраска по коду цвета, КМ — материал без кода цвета; «Помещения» — номера по экспликации; количества — по ведомости отделки помещений (лист 57).
3. Марки позиций: один префикс — один вид позиций на весь альбом (двери Д, окна ОК, мебель М, сантехприборы П, декор ДК, текстиль Т, колерная карта К и КМ, радиаторы РО, розетки Р, выключатели S, светильники Св; стояки — «Ст» и система, например «Ст К1-1»). Совпадение префиксов у разных видов — замечание к исходным данным, при выпуске исправляется в модели.

Допущения и предложения на листе. Основа листа: размеры сняты с растрового плана заказчика без размеров: масштаб восстановлен по площадям помещений (≈ 11,8 мм на пиксель), контрольный обмер не выполнен (К-1); высота потолка 2700 мм принята: на плане заказчика её нет (К-2); толщины стен 300 / 120 мм приняты по плану заказчика, не замерены (К-1); разрешённая мощность 15 кВт принята по типовым ТУ для квартиры, ТУ заказчиком не переданы (К-4); подрайон климата не задан — принят не северный (жилые от 2,5 м) (К-9). Знак «**» — предложено, не утверждено (согласовать): пол пом. 1–3, 8, 9, Св5, ИП3, ИП4, Р12; К-5: М2, М3, М1. См. лист открытых вопросов (лист 6, записи К-1, К-2, К-4, К-5; лист 7, запись К-9; лист 8, записи ИЗ-4, ИЗ-5).


Изм.	Кол.уч	Лист	№ док.	Подп.	Дата	ГД-2026-007-АИ			
						Квартира 65 м²			
						Общая площадь 65,24* м² · * размеры со скана, не замерены (реестр — л. 6–8, К-1)			
Разраб.		Кырлан А.С.			14.11.26	Дизайн-проект интерьера	Стадия	Лист	Листов
Пров.							РП	79	117
ГИП									
						Реестр марок отделки и позиций альбома	Кырлан Александр Сергеевич		
Н. контр.						М б/м			
Утв.									

выпуск 14.11.2026 № 9cc0b98f36 · стр. 88 из 139

Схема расположения развёрток и узлов

План квартиры: марки развёрток по помещениям, выноски узлов, ведомость «марка → лист»

ПРЕДВАРИТЕЛЬНО · не для производства работ · открыто пунктов: 14 (реестр — л. 6–8)

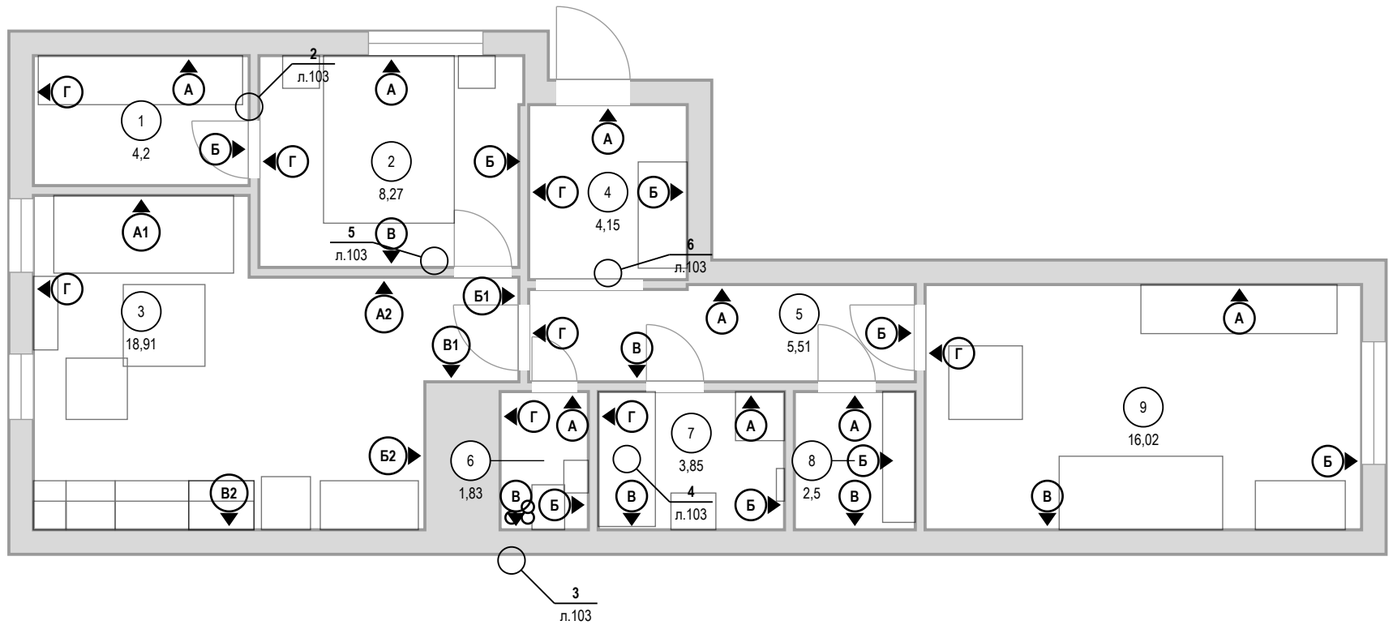

Развёртки и узлы: марка → лист

Марка	Помещение / узел	Лист
А	Гардеробная (пом. 1)	81
Б, Г	Гардеробная (пом. 1)	82
А	Спальня (пом. 2)	83
Б	Спальня (пом. 2)	84
В, Г	Спальня (пом. 2)	85
В2	Кухня-гостиная (пом. 3)	86
Г	Кухня-гостиная (пом. 3)	87
А1, А2	Кухня-гостиная (пом. 3)	88
Б1, Б2, В1	Кухня-гостиная (пом. 3)	89
А, Б	Прихожая (пом. 4)	90
Г	Прихожая (пом. 4)	91
А, Б	Коридор (пом. 5)	92
В, Г	Коридор (пом. 5)	93
А, Б	Санузел (пом. 6)	94
В, Г	Санузел (пом. 6)	95
А, Б	Ванная (пом. 7)	96
В, Г	Ванная (пом. 7)	97
А, Б, В	Кладовая (пом. 8)	98
А	Детская (пом. 9)	99
Б	Детская (пом. 9)	100
В	Детская (пом. 9)	101
Г	Детская (пом. 9)	102
узел 1	Порог 15 мм: мокрая зона — смежное помещение	103
узел 2	Дверь скрытого монтажа в плоскости стены, плинтус	103
узел 3	Короб стояков К1-1 с люком и звукоизоляцией	103
узел 4	Гидроизоляция санузла: заход на стены 200 мм, примыкание ванны	103
узел 5	Плинтус МДФ 69×16 мм у окрашенной стены по доске (ламинату)	103
узел 6	Плинтус МДФ 69×16 мм у окрашенной стены по керамограниту (плитке)	103

Допущения и предложения на листе

Основа листа: размеры сняты с растрового плана заказчика без размеров: масштаб восстановлен по площадям помещений (≈ 11,8 мм на пиксель), контрольный обмер не выполнен (К-1); высота потолка 2700 мм принята: на плане заказчика её нет (К-2); толщины стен 300 / 120 мм приняты по плану заказчика, не замерены (К-1); разрешённая мощность 15 кВт принята по типовым ТУ для квартиры, ТУ заказчиком не переданы (К-4); подрайон климата не задан — принят не северный (жилые от 2,5 м) (К-9).
См. лист открытых вопросов (лист 6, записи К-1, К-2, К-4; лист 7, запись К-9).

Условные обозначения

- А — марка развёртки: буква стены, стрелка — взгляд
- выноска узла: над полкой — узел, под полкой — лист
- 1 — номер помещения, площадь м²

1000 мм · печать 1:1

Примечания

1. Развёртки — вид на стену изнутри помещения; буквы стен — одна система на весь альбом (как на листах выводов, плитки и отделки).
2. Стены без электроточек, мебели, декора и акцентной отделки развёрток не имеют: их отделка — по ведомости отделки помещений.
3. Узлы — на листе узлов; места применения — по выноскам этого листа и ведомости «марка → лист».

Изм.	Кол.уч	Лист	№ док.	Подп.	Дата
Разраб.		Кырлан А.С.			14.11.26
Пров.					
ГИП					
Н. контр.					
Утв.					

ГД-2026-007-АИ

Квартира 65 м²

Общая площадь 65,24* м² · * размеры со скана, не замерены (реестр — л. 6–8, К-1)

Дизайн-проект интерьера	Стадия	Лист	Листов
	РП	80	117
Схема расположения развёрток и узлов М 1:75	**Кырлан Александр Сергеевич**		


выпуск 14.11.2026 № 9cc0b98f36 · стр. 89 из 139

Развёртка стены А. Гардеробная (пом. 1)

Гардеробная (пом. 1) · вид изнутри помещения · размеры в мм, отметки в м

ПРЕДВАРИТЕЛЬНО · не для производства работ · открыто пунктов: 14 (реестр — л. 6–8)


Стена А (М 1:20)

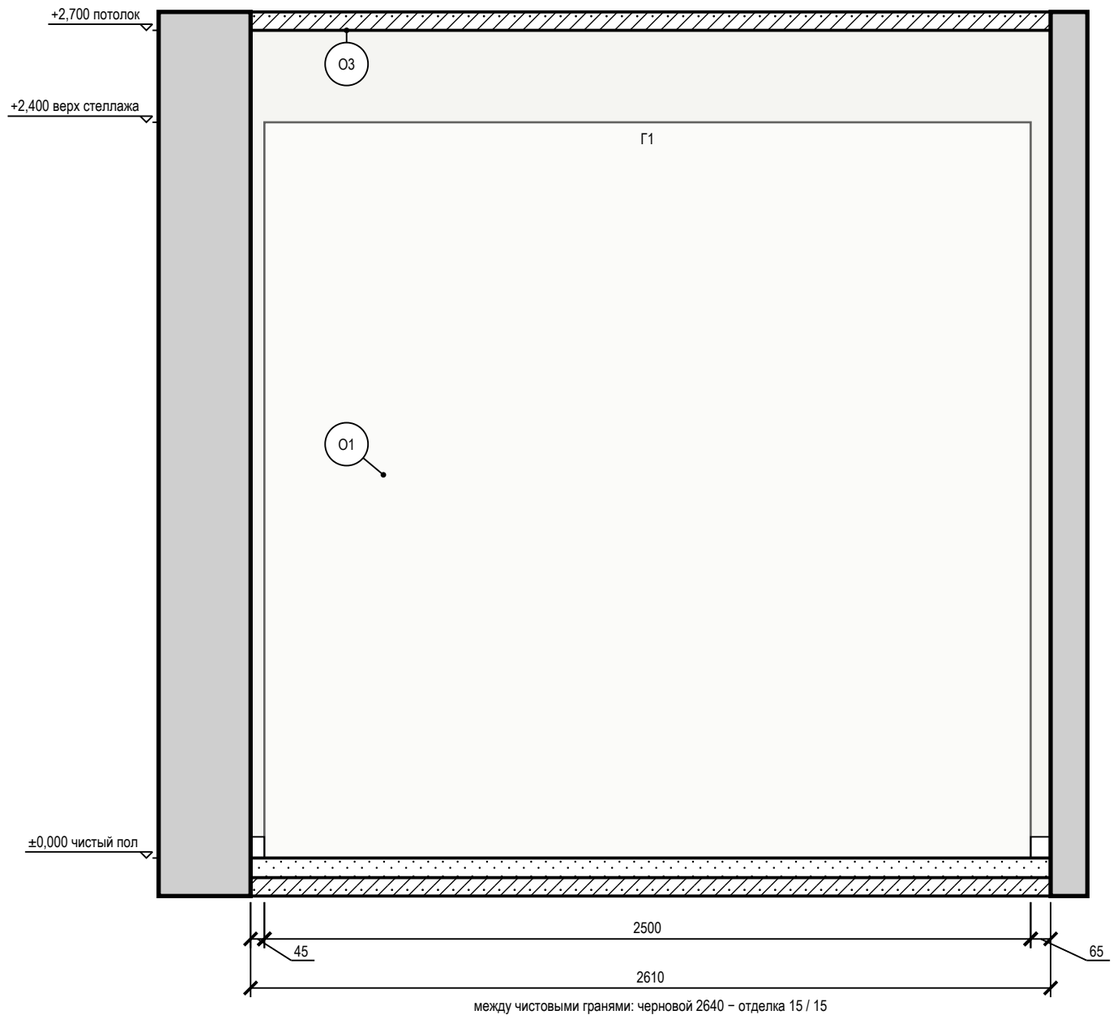

Ведомость отделки (на листе)

Марка	Поверхность	Материал, изделие	Цвет, код	Кол.
О1	стены	окраска, Tikkurila Harmony, матовая, подготовка Q3	Tikkurila V503 «Winter»	7 м²
О2	плинтус	плинтус МДФ, Orac Decor Contour (Luxxus), h 69 мм, SX165	Tikkurila V503 «Winter»	0,1 м
О3	потолок	окраска, Tikkurila Anti-Reflex 2, глубокоматовая, подготовка Q3	Tikkurila V503 «Winter»	4,2 м²

Схема развёрток (М 1:50)

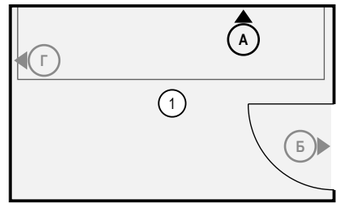

Условные обозначения

- мебель и приборы — фасад по расстановке (условно)
- стены и перекрытия в сечении
- окраска: тон — цвет по коду производителя (условно)
- О1 — марка отделки по реестру отделки альбома
- А — марка развёртки: буква стены, стрелка — взгляд

Ведомость изделий и проёмов (на листе)

Марка	Изделие, проём	На виде Ш×В, мм	Низ, мм
Г1	система хранения: штанги, полки, ящики	2500×2400	0

Примечания

1. Развёртки — вид на стену изнутри помещения, по часовой стрелке; расположение — на схеме листа и на листе 80; размеры — в мм по чистовым поверхностям; отметки — в м от ±0,000; высоты Н — от чистого пола помещения до оси изделия, у декора — до центра.
2. Схема мебели, приборов и декора не является технической документацией для производства мебели; габариты — по паспортам изделий.

Допущения и предложения на листе

Основа листа: размеры сняты с растрового плана заказчика без размеров: масштаб восстановлен по площадям помещений (≈ 11,8 мм на пиксель), контрольный обмер не выполнен (К-1); высота потолка 2700 мм принята: на плане заказчика её нет (К-2); толщины стен 300 / 120 мм приняты по плану заказчика, не замерены (К-1); разрешённая мощность 15 кВт принята по типовым ТУ для квартиры, ТУ заказчиком не переданы (К-4); подрайон климата не задан — принят не северный (жилые от 2,5 м) (К-9).
См. лист открытых вопросов (лист 6, записи К-1, К-2, К-4; лист 7, запись К-9).

1000 мм · печать 1:1

Изм.	Кол.уч	Лист	№ док.	Подп.	Дата
Разраб.		Кырлан А.С.			14.11.26
Пров.					
ГИП					
Н. контр.					
Утв.					

ГД-2026-007-АИ

Квартира 65 м²

Общая площадь 65,24* м² · * размеры со скана, не замерены (реестр — л. 6–8, К-1)

Дизайн-проект интерьера

Стадия	Лист	Листов
РП	81	117

Развёртка стены А. Гардеробная (пом. 1)

М 1:20

Кырлан Александр Сергеевич


выпуск 14.11.2026 № 9cc0b98f36 · стр. 90 из 139

Развёртки стен Б, Г. Гардеробная (пом. 1)

Гардеробная (пом. 1) · вид изнутри помещения · размеры в мм, отметки в м


ПРЕДВАРИТЕЛЬНО · не для производства работ · открыто пунктов: 14 (реестр — л. 6–8)

Стена Б (М 1:20)

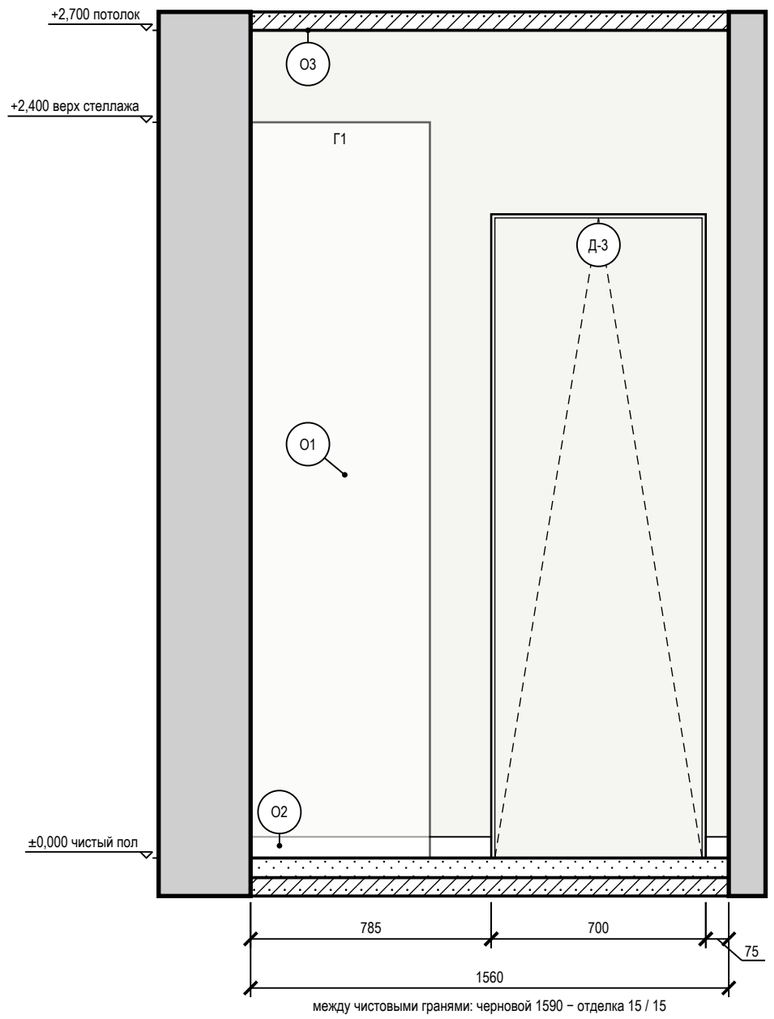

между чистовыми гранями: черновой 1590 − отделка 15 / 15

Стена Г (М 1:20)

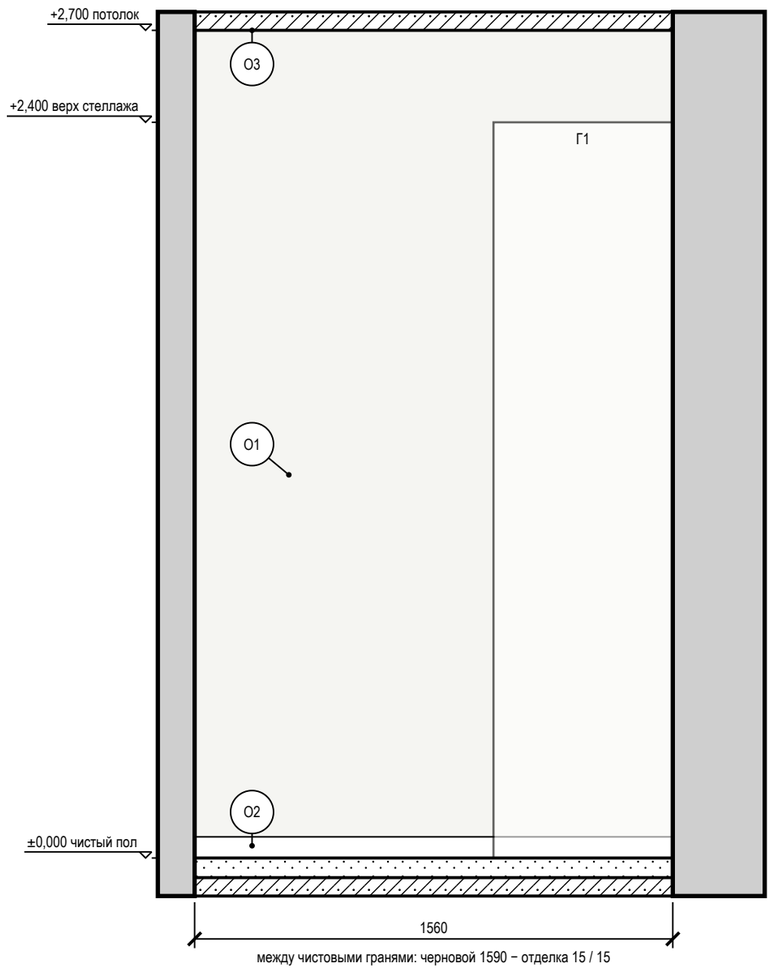

между чистовыми гранями: черновой 1590 − отделка 15 / 15


Условные обозначения

- мебель и приборы — фасад по расстановке (условно)
- дверь скрытого монтажа: полотно в плоскости стены (узел — на листе узлов)
- стены и перекрытия в сечении
- окраска: тон — цвет по коду производителя (условно)
- О1 — марка отделки по реестру отделки альбома
- А — марка развёртки: буква стены, стрелка — взгляд

Ведомость отделки (на листе)

Марка	Поверхность	Материал, изделие	Цвет, код	Кол.
О1	стены	окраска, Tikkurila Harmony, матовая, подготовка Q3	Tikkurila V503 «Winter»	7 м²
О2	плинтус	плинтус МДФ, Orac Decor Contour (Luxxus), h 69 мм, SX165	Tikkurila V503 «Winter»	2,4 м
О3	потолок	окраска, Tikkurila Anti-Reflex 2, глубокоматовая, подготовка Q3	Tikkurila V503 «Winter»	4,2 м²

Схема развёрток (М 1:50)

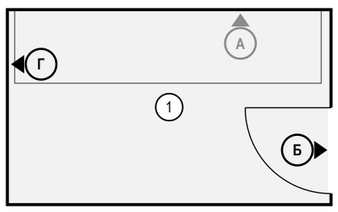

Ведомость изделий и проёмов (на листе)

Стена	Марка	Изделие, проём	На виде Ш×В, мм	Низ, мм
Б	Г1	система хранения: штанги, полки, ящики	585×2400	0
Б	Д-3	дверь скрытого монтажа	700×2100	0
Г	Г1	система хранения: штанги, полки, ящики	585×2400	0

Примечания

1. Развёртки — вид на стену изнутри помещения, по часовой стрелке; расположение — на схеме листа и на листе 80; размеры — в мм по чистовым поверхностям; отметки — в м от ±0,000; высоты Н — от чистого пола помещения до оси изделия, у декора — до центра.
2. Схема мебели, приборов и декора не является технической документацией для производства мебели; габариты — по паспортам изделий.
3. Двери скрытого монтажа — полотно в плоскости стены, отделка стены по полотну, плинтус прерывается у короба (узел — на листе узлов).

Допущения и предложения на листе

Основа листа: размеры сняты с растрового плана заказчика без размеров: масштаб восстановлен по площадям помещений (≈ 11,8 мм на пиксель), контрольный обмер не выполнен (К-1); высота потолка 2700 мм принята: на плане заказчика её нет (К-2); толщины стен 300 / 120 мм приняты по плану заказчика, не замерены (К-1); разрешённая мощность 15 кВт принята по типовым ТУ для квартиры, ТУ заказчиком не переданы (К-4); подрайон климата не задан — принят не северный (жилые от 2,5 м) (К-9).
См. лист открытых вопросов (лист 6, записи К-1, К-2, К-4; лист 7, запись К-9).

1000 мм · печать 1:1

Изм.	Кол.уч	Лист	№ док.	Подп.	Дата
Разраб.		Кырлан А.С.			14.11.26
Пров.					
ГИП					
Н. контр.					
Утв.					

ГД-2026-007-АИ

Квартира 65 м²

Общая площадь 65,24* м² · * размеры со скана, не замерены (реестр — л. 6–8, К-1)

Дизайн-проект интерьера

Стадия	Лист	Листов
РП	82	117

Развёртки стен Б, Г. Гардеробная (пом. 1)

М 1:20

Кырлан Александр Сергеевич


выпуск 14.11.2026 № 9cc0b98f36 · стр. 91 из 139

Развёртка стены А. Спальня (пом. 2)

Спальня (пом. 2) · вид изнутри помещения · размеры в мм, отметки в м

ПРЕДВАРИТЕЛЬНО · не для производства работ · открыто пунктов: 14 (реестр — л. 6–8)

Стена А (М 1:20)

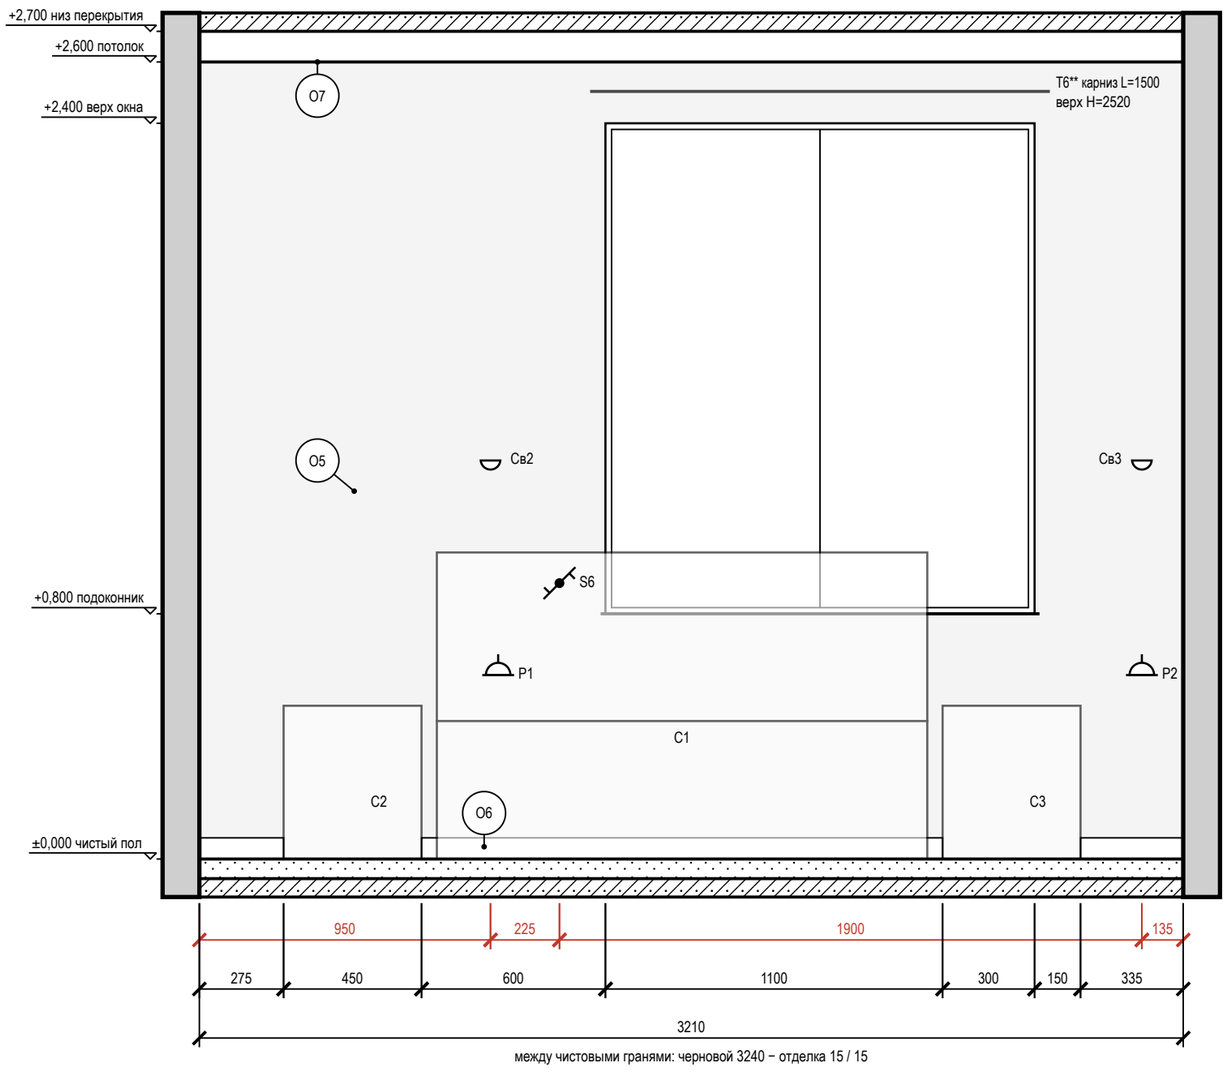

между чистовыми гранями: черновой 3240 − отделка 15 / 15

Ведомость точек и выводов

Марка	Что это	Гр.	H, мм	От угла, мм	Примечание
Св2	светильник настенный	1	1300	950	
P1	розетка	4	600	975	
S6	выключатель	1	900	1175	
P2	розетка	4	600	3075	
Св3	светильник настенный	1	1300	3075	


Условные обозначения

- розетка с заземляющим контактом; у знака — марка, ×N постов в рамке, гр. — группа щита, H — высота оси, мм
- выключатель одноклавишный
- выключатель с проходной или перекрёстной клавишей (обратный флажок); тип клавиши — в подписи
- светильник настенный (бра), H — высота оси
- привязки точек и выводов от угла и от пола, мм
- мебель и приборы — фасад по расстановке (условно)
- карниз (шина) и шторы в собранном виде: марка T, длина L, верх H
- окно: проём, рама, подоконник
- стены и перекрытия в сечении
- О1 — марка отделки по реестру отделки альбома
- А — марка развёртки: буква стены, стрелка — взгляд

Ведомость отделки (на листе)

Марка	Поверхность	Материал, изделие	Цвет, код	Кол.
О5	стены	окраска, Tikkurila, глубокоматовая, подготовка Q3	NCS S 1502-Y50R	6,1 м²
О6	плинтус	плинтус МДФ, Orac Decor Contour (Luxxus), h 69 мм, SX165, шелковисто-матовая	NCS S 0300-N	2,3 м
О7	потолок	окраска, Tikkurila, глубокоматовая	NCS S 0300-N	8,3 м²

Схема развёрток (М 1:50)

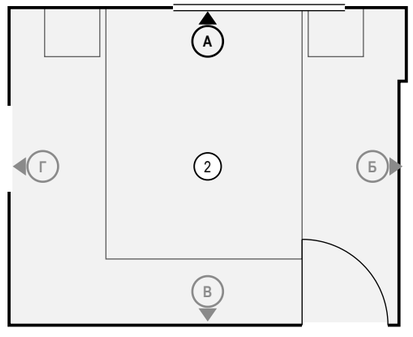

Примечания

1. Развёртки — вид на стену изнутри помещения, по часовой стрелке; расположение — на схеме листа и на листе 80; размеры — в мм по чистовым поверхностям; отметки — в м от ±0,000; высоты H — от чистого пола помещения до оси изделия, у декора — до центра.
2. Красная цепочка — привязки электроточек и выводов по осям от угла чистовых стен; высота H — у знака, от чистого пола до оси; высоты мебели, проёмов и границ отделки — колонкой отметок слева. У знака — короткая марка; назначение, группа щита, высота и привязка каждой точки и вывода — в «Ведомости точек и выводов» под видами (каждая точка — строка).
3. У знака электроточки: марка (P — розетка, S — выключатель, Св — светильник, ЭВ — вывод кабеля), ×N — число постов в рамке, гр. — группа щита, H — высота оси от чистого пола, мм; группы по клавишам выключателя — на листе выключателей.
4. Схема мебели, приборов и декора не является технической документацией для производства мебели; габариты — по паспортам изделий.
5. Карнизы (шины) — по ведомости текстиля декоратора: длина L и верх H на развёртке — те же числа, что в ведомости; крепление — до окраски потолка.

Допущения и предложения на листе

Основа листа: размеры сняты с растрового плана заказчика без размеров: масштаб восстановлен по площадям помещений (≈ 11,8 мм на пиксель), контрольный обмер не выполнен (К-1); высота потолка 2700 мм принята: на плане заказчика её нет (К-2); толщины стен 300 / 120 мм приняты по плану заказчика, не замерены (К-1); разрешённая мощность 15 кВт принята по типовым ТУ для квартиры, ТУ заказчиком не переданы (К-4); подрайон климата не задан — принят не северный (жилые от 2,5 м) (К-9).

Знак «**» — предложение проектировщика, заказчиком не утверждено (согласовать с заказчиком): ИЗ-4: Т6.

См. лист открытых вопросов (лист 6, записи К-1, К-2, К-4; лист 7, запись К-9; лист 8, запись ИЗ-4).

1000 мм · печать 1:1

Изм.	Кол.уч	Лист	№ док.	Подп.	Дата
Разраб.		Кырлан А.С.			14.11.26
Пров.					
ГИП					
Н. контр.					
Утв.					

ГД-2026-007-АИ

Квартира 65 м²

Общая площадь 65,24* м² · * размеры со скана, не замерены (реестр — л. 6–8, К-1)

Дизайн-проект интерьера

Стадия	Лист	Листов
РП	83	117

Развёртка стены А. Спальня (пом. 2)

М 1:20

Кырлан Александр Сергеевич


выпуск 14.11.2026 № 9cc0b98f36 · стр. 92 из 139

Развёртка стены Б. Спальня (пом. 2)

Спальня (пом. 2) · вид изнутри помещения · размеры в мм, отметки в м

ПРЕДВАРИТЕЛЬНО · не для производства работ · открыто пунктов: 14 (реестр — л. 6–8)

Стена Б (М 1:20)

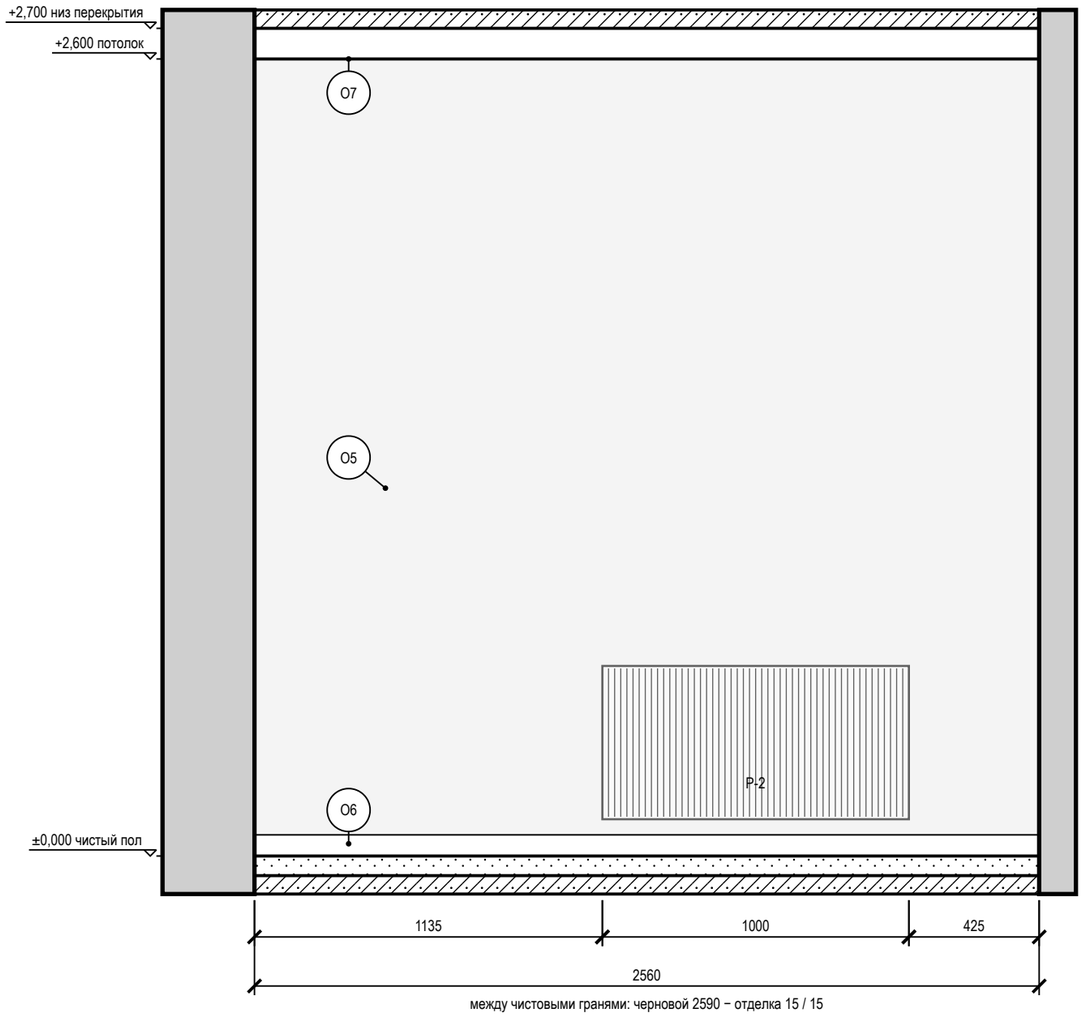


между чистовыми гранями: черновой 2590 − отделка 15 / 15

Ведомость отделки (на листе)

Марка	Поверхность	Материал, изделие	Цвет, код	Кол.
О5	стены	окраска, Tikkurila, глубокоматовая, подготовка Q3	NCS S 1502-Y50R	6,7 м²
О6	плинтус	плинтус МДФ, Orac Decor Contour (Luxxus), h 69 мм, SX165, шелковисто-матовая	NCS S 0300-N	2,6 м
О7	потолок	окраска, Tikkurila, глубокоматовая	NCS S 0300-N	8,3 м²

Схема развёрток (М 1:50)

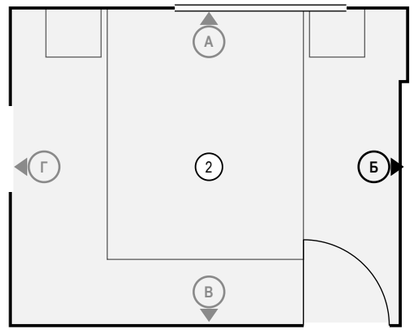

Условные обозначения

- мебель и приборы — фасад по расстановке (условно)
- радиатор отопления; марка — по плану отопления
- стены и перекрытия в сечении
- О1 — марка отделки по реестру отделки альбома
- А — марка развёртки: буква стены, стрелка — взгляд

Ведомость изделий и проёмов (на листе)

Марка	Изделие, проём	На виде Ш×В, мм	Низ, мм
Р-2	радиатор отопления	1000×500	120

Примечания

1. Развёртки — вид на стену изнутри помещения, по часовой стрелке; расположение — на схеме листа и на листе 80; размеры — в мм по чистовым поверхностям; отметки — в м от ±0,000; высоты Н — от чистого пола помещения до оси изделия, у декора — до центра.
2. Схема мебели, приборов и декора не является технической документацией для производства мебели; габариты — по паспортам изделий.

Допущения и предложения на листе

Основа листа: размеры сняты с растрового плана заказчика без размеров: масштаб восстановлен по площадям помещений (≈ 11,8 мм на пиксель), контрольный обмер не выполнен (К-1); высота потолка 2700 мм принята: на плане заказчика её нет (К-2); толщины стен 300 / 120 мм приняты по плану заказчика, не замерены (К-1); разрешённая мощность 15 кВт принята по типовым ТУ для квартиры, ТУ заказчиком не переданы (К-4); подрайон климата не задан — принят не северный (жилые от 2,5 м) (К-9).
См. лист открытых вопросов (лист 6, записи К-1, К-2, К-4; лист 7, запись К-9).

1000 мм · печать 1:1

Изм.	Кол.уч	Лист	№ док.	Подп.	Дата
Разраб.		Кырлан А.С.			14.11.26
Пров.					
ГИП					
Н. контр.					
Утв.					

ГД-2026-007-АИ

Квартира 65 м²

Общая площадь 65,24* м² · * размеры со скана, не замерены (реестр — л. 6–8, К-1)

Дизайн-проект интерьера

Стадия	Лист	Листов
РП	84	117

Развёртка стены Б. Спальня (пом. 2)

М 1:20

Кырлан Александр Сергеевич


выпуск 14.11.2026 № 9cc0b98f36 · стр. 93 из 139

Развёртки стен В, Г. Спальня (пом. 2)

Спальня (пом. 2) · вид изнутри помещения · размеры в мм, отметки в м


ПРЕДВАРИТЕЛЬНО · не для производства работ · открыто пунктов: 14 (реестр — л. 6–8)

Стена В (М 1:25)

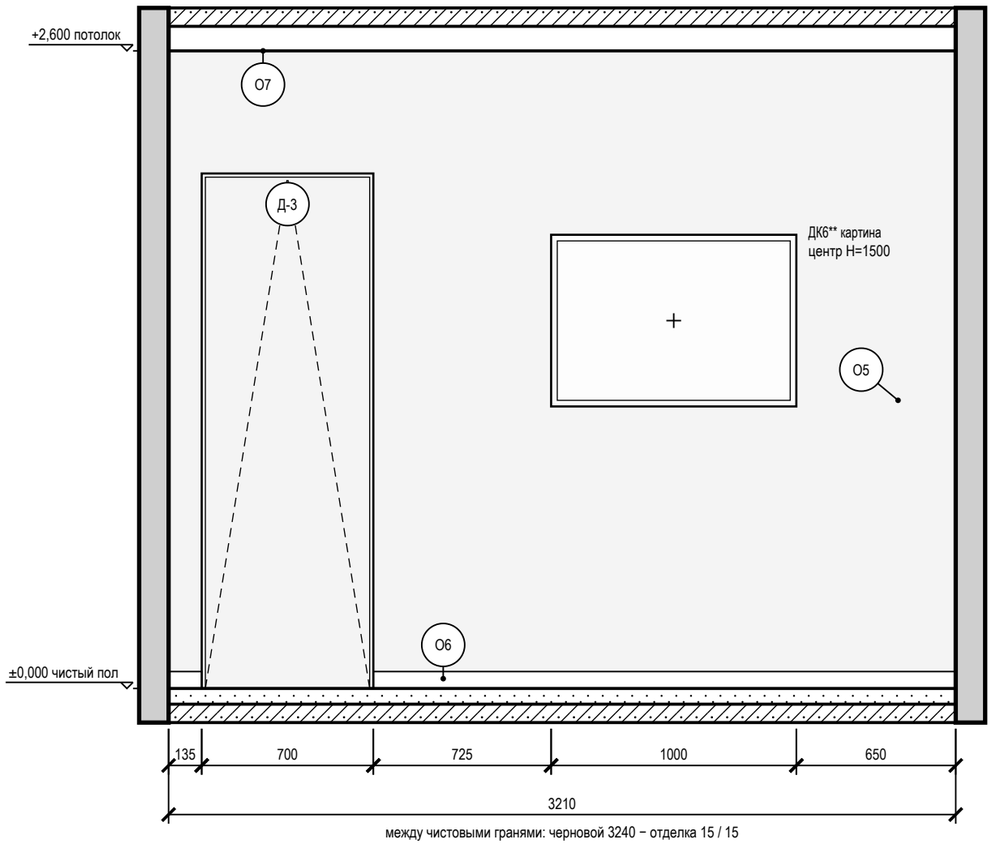

между чистовыми гранями: черновой 3240 − отделка 15 / 15

Стена Г (М 1:25)

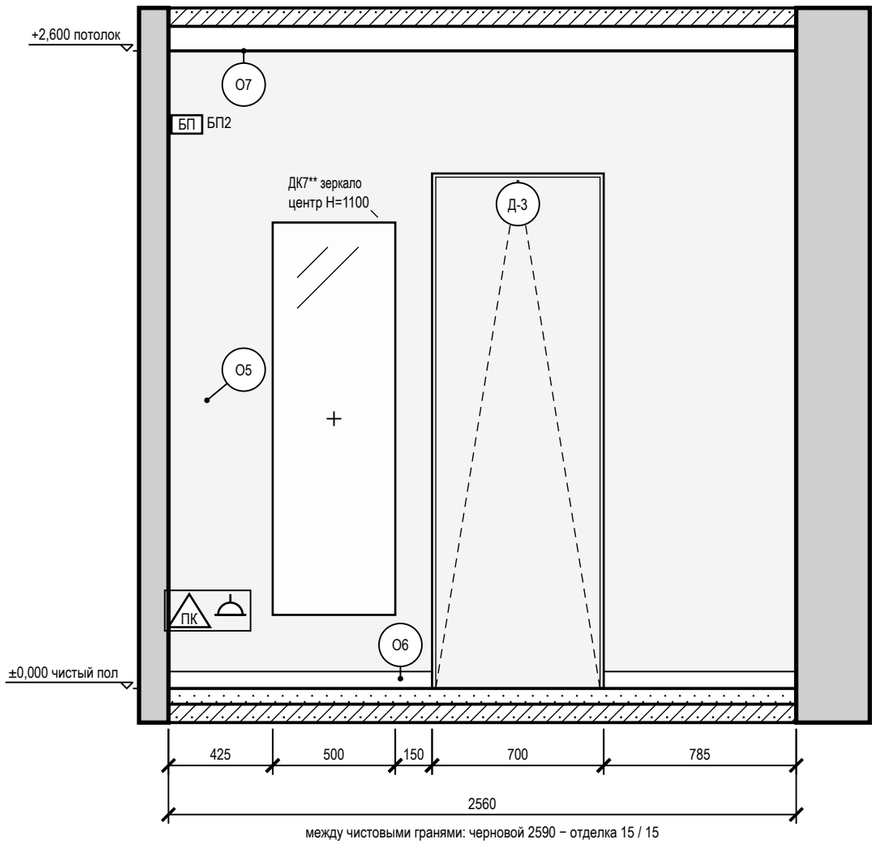

между чистовыми гранями: черновой 2590 − отделка 15 / 15


Ведомость точек и выводов

Стена	Марка	Что это	Гр.	Н, мм	От угла, мм	Примечание
Г	LAN2	розетка RJ45: рабочее место, ТВ		300	75	
Г	БП2	блок питания LED	1	2300	75	
Г	Р3	розетка: комод, зарядка	4	300	175	

Условные обозначения

- розетка с заземляющим контактом; у знака — марка, ×N постов в рамке, гр. — группа щита, Н — высота оси, мм
- БП — блок питания LED, с доступом (люк от 100×100 мм)
- ПК — розетка компьютерная RJ45
- привязки точек и выводов от угла и от пола, мм
- мебель и приборы — фасад по расстановке (условно)
- картина (декор): марка Д, крест — центр, Н — высота центра, мм
- зеркало: марка Д, крест — центр, Н — высота центра, мм
- дверь скрытого монтажа: полотно в плоскости стены (узел — на листе узлов)
- стены и перекрытия в сечении
- О1 — марка отделки по реестру отделки альбома
- А — марка развёртки: буква стены, стрелка — взгляд

Схема развёрток (М 1:100)

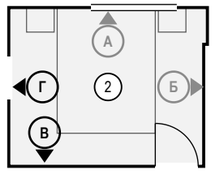

Примечания

1. Развёртки — вид на стену изнутри помещения, по часовой стрелке; расположение — на схеме листа и на листе 80; размеры — в мм по чистовым поверхностям; отметки — в м от ±0,000; высоты Н — от чистого пола помещения до оси изделия, у декора — до центра.
2. Красная цепочка — привязки электроточек и выводов по осям от угла чистовых стен; высота Н — у знака, от чистого пола до оси; высоты мебели, проёмов и границ отделки — колонкой отметок слева. У знака — короткая марка; назначение, группа щита, высота и привязка каждой точки и вывода — в «Ведомости точек и выводов» под видами (каждая точка — строка).
3. Отделка стен — по ведомости отделки помещений, лист 57.
4. У знака электроточки: марка (Р — розетка, S — выключатель, Св — светильник, ЭВ — вывод кабеля), ×N — число постов в рамке, гр. — группа щита, Н — высота оси от чистого пола, мм; группы по клавишам выключателя — на листе выключателей.
5. Схема мебели, приборов и декора не является технической документацией для производства мебели; габариты — по паспортам изделий.
6. Картины и зеркала крепить к основанию по паспорту изделия (закладные и анкеры — в перечне скрытых работ); крест — ось центра предмета.
7. Двери скрытого монтажа — полотно в плоскости стены, отделка стены по полотну, плинтус прерывается у короба (узел — на листе узлов).
8. Часть марок не уместилась у знаков: коды, высоты и привязки этих позиций — в ведомости точек и выводов под видами.

Допущения и предложения на листе. Знак «**» предложено (согласовать). См. лист открытых вопросов (листы 6–8).

1000 мм · печать 1:1

Изм.	Кол.уч	Лист	№ док.	Подп.	Дата
Разраб.		Кырлан А.С.			14.11.26
Пров.					
ГИП					
Н. контр.					
Утв.					

ГД-2026-007-АИ

Квартира 65 м²

Общая площадь 65,24* м² · * размеры со скана, не замерены (реестр — л. 6–8, К-1)

Дизайн-проект интерьера

Стадия	Лист	Листов
РП	85	117

Развёртки стен В, Г. Спальня (пом. 2)

М 1:25

Кырлан Александр Сергеевич


выпуск 14.11.2026 № 9cc0b98f36 · стр. 94 из 139

Развёртка стены В2. Кухня-гостиная (пом. 3), кухонный фронт

Кухня-гостиная (пом. 3) · вид изнутри помещения · размеры в мм, отметки в м

ПРЕДВАРИТЕЛЬНО · не для производства работ · открыто пунктов: 14 (реестр — л. 6–8)

Стена В2 (М 1:25)

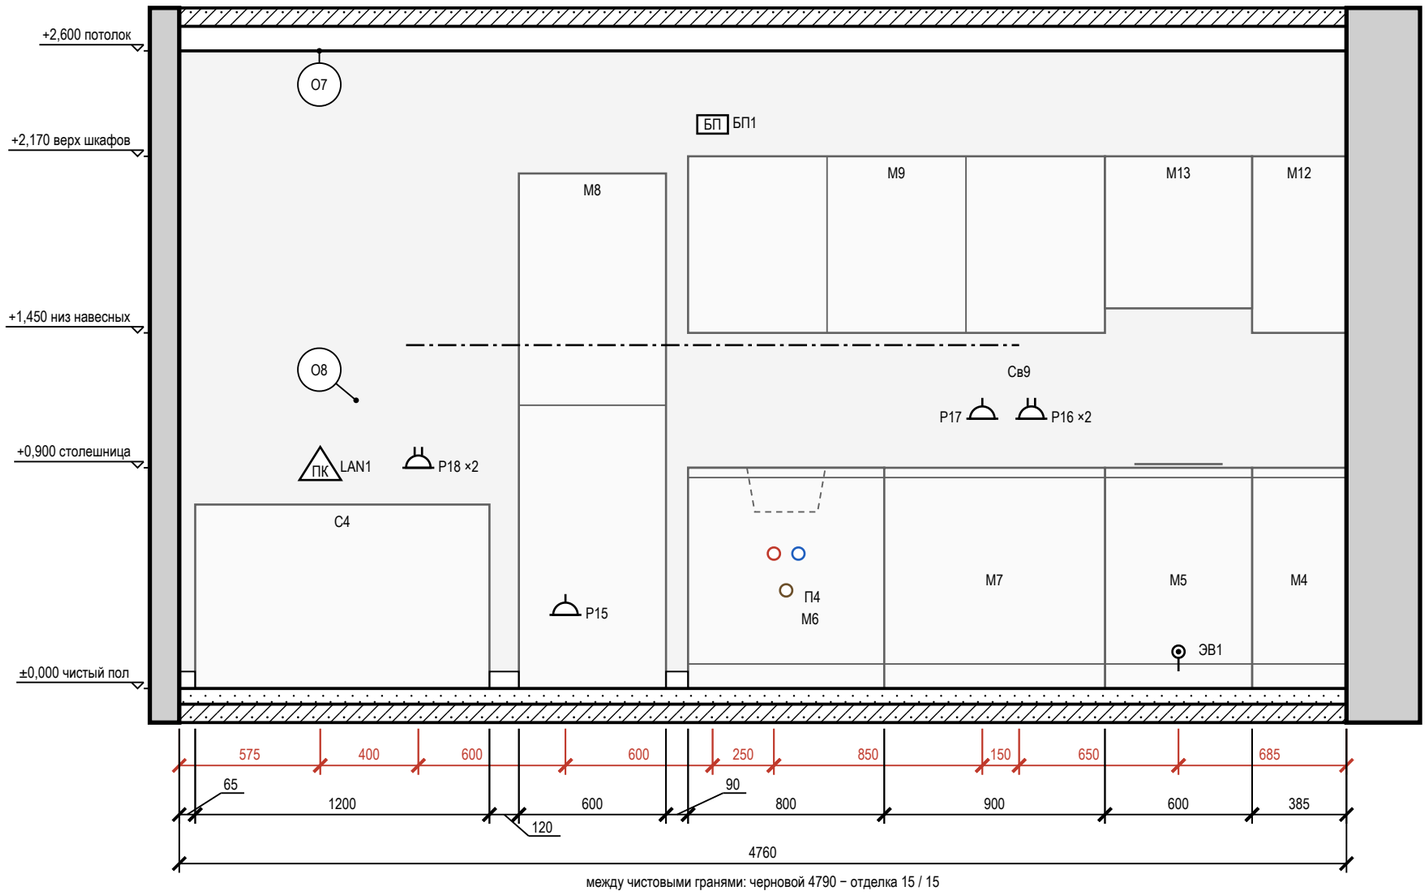

между чистовыми гранями: черновой 4790 − отделка 15 / 15

Ведомость точек и выводов

Марка	Что это	Гр.	Н, мм	От угла, мм	Примечание
LAN1	розетка RJ45: рабочее место		900	575	
Р18	розетка: рабочее место	4	900	975	рамка 2 поста
Р15	розетка: холодильник	2	300	1575	
БП1	блок питания LED	1	2300	2175	
Т3-1	горячая вода — мойка кухонная		550	2425	межос. 100
К1-1	канализация — мойка кухонная		400	2475	Ø50
В1-1	холодная вода — мойка кухонная		550	2525	межос. 100
Р17	розетка: рабочая зона	2	1100	3275	
Св9	светильник настенный	1	1400	3425	лента 925–3425 от угла
Р16	розетка: рабочая зона	2	1100	3475	рамка 2 поста
ЭВ1	вывод кабеля: варочная панель	3	150	4075	

Условные обозначения

- розетка с заземляющим контактом; у знака марка, ×N — постов в рамке, гр. — группа щита, Н — высота оси, мм
- вывод кабеля для подключения прибора (без розетки), марка ЭВ
- светодиодная лента в профиле / в карнизе короба
- БП — блок питания LED, с доступом (люк от 100×100 мм)
- ПК — розетка компьютерная RJ45
- вывод В1 (код — в ведомости привязок)
- вывод Т3 (код — в ведомости привязок)
- вывод К1 (код — в ведомости привязок)
- привязки точек и выводов от угла и от пола, мм
- мебель и приборы — фасад по расстановке (условно)
- стены и перекрытия в сечении
- О1 — марка отделки по реестру отделки альбома
- А — марка развёртки: буква стены, стрелка взгляд

Ведомость отделки (на листе)

Марка	Поверхность	Материал, изделие	Цвет, код	Кол.
О6	плинтус	плинтус МДФ, Orac Decor Contour (Luxxus), h 69 мм, SX165, шелковисто-матовая	NCS S 0300-N	0,3 м
О7	потолок	окраска, Tikkurila, глубокоматовая	NCS S 0300-N	18,9 м²
О8	стены	окраска, Tikkurila, шелковисто-матовая, подготовка Q3	NCS S 1002-Y50R	12,4 м²

Примечания

1. Развёртки — вид на стену изнутри помещения, по часовой стрелке; расположение — на схеме листа и на листе 80; размеры — в мм по чистовым поверхностям; отметки — в м от ±0,000; высоты Н — от чистого пола помещения до оси изделия, у декора — до центра.
2. Красная цепочка — привязки электроточек и выводов по осям от угла чистовых стен; высота Н — у знака, от чистого пола до оси; высоты мебели, проёмов и границ отделки — колонкой отметок слева. У знака — короткая марка; назначение, группа щита, высота и привязка каждой точки и вывода — в «Ведомости точек и выводов» под видами (каждая точка — строка).
3. У знака электроточки: марка (Р — розетка, S — выключатель, Св — светильник, ЭВ — вывод кабеля), ×N — число постов в рамке, гр. — группа щита, Н — высота оси от чистого пола, мм; группы по клавишам выключателя — на листе выключателей.
4. Схема мебели, приборов и декора не является технической документацией для производства мебели; габариты — по паспортам изделий.
5. Выводы кухонной техники — по утверждённому проекту кухни: привязки выводов даются от осей модулей гарнитура.
6. Часть марок не уместилась у знаков: коды, высоты и привязки этих позиций — в ведомости точек и выводов под видами.

Допущения и предложения на листе

Основа листа: размеры сняты с растрового плана заказчика без размеров: масштаб восстановлен по площадям помещений (≈ 11,8 мм на пиксель), контрольный обмер не выполнен (К-1); высота потолка 2700 мм принята: на плане заказчика её нет (К-2); толщины стен 300 / 120 мм приняты по плану заказчика, не замерены (К-1); разрешённая мощность 15 кВт принята по типовым ТУ для квартиры, ТУ заказчиком не переданы (К-4); подрайон климата не задан — принят не северный (жилые от 2,5 м) (К-9).

См. лист открытых вопросов (лист 6, записи К-1, К-2, К-4; лист 7, запись К-9).

1000 мм · печать 1:1

Изм.	Кол.уч	Лист	№ док.	Подп.	Дата
Разраб.		Кырлан А.С.			14.11.26
Пров.					
ГИП					
Н. контр.					
Утв.					

ГД-2026-007-АИ

Квартира 65 м²

Общая площадь 65,24* м² · * размеры со скана, не замерены (реестр — л. 6–8, К-1)

Дизайн-проект интерьера

Стадия	Лист	Листов
РП	86	117

Развёртка стены В2. Кухня-гостиная (пом. 3), кухонный фронт

М 1:25

Кырлан Александр Сергеевич


выпуск 14.11.2026 № 9cc0b98f36 · стр. 95 из 139

Развёртка стены Г. Кухня-гостиная (пом. 3), кухонный фронт

Кухня-гостиная (пом. 3) · вид изнутри помещения · размеры в мм, отметки в м

ПРЕДВАРИТЕЛЬНО · не для производства работ · открыто пунктов: 14 (реестр — л. 6–8)

Стена Г (М 1:20)

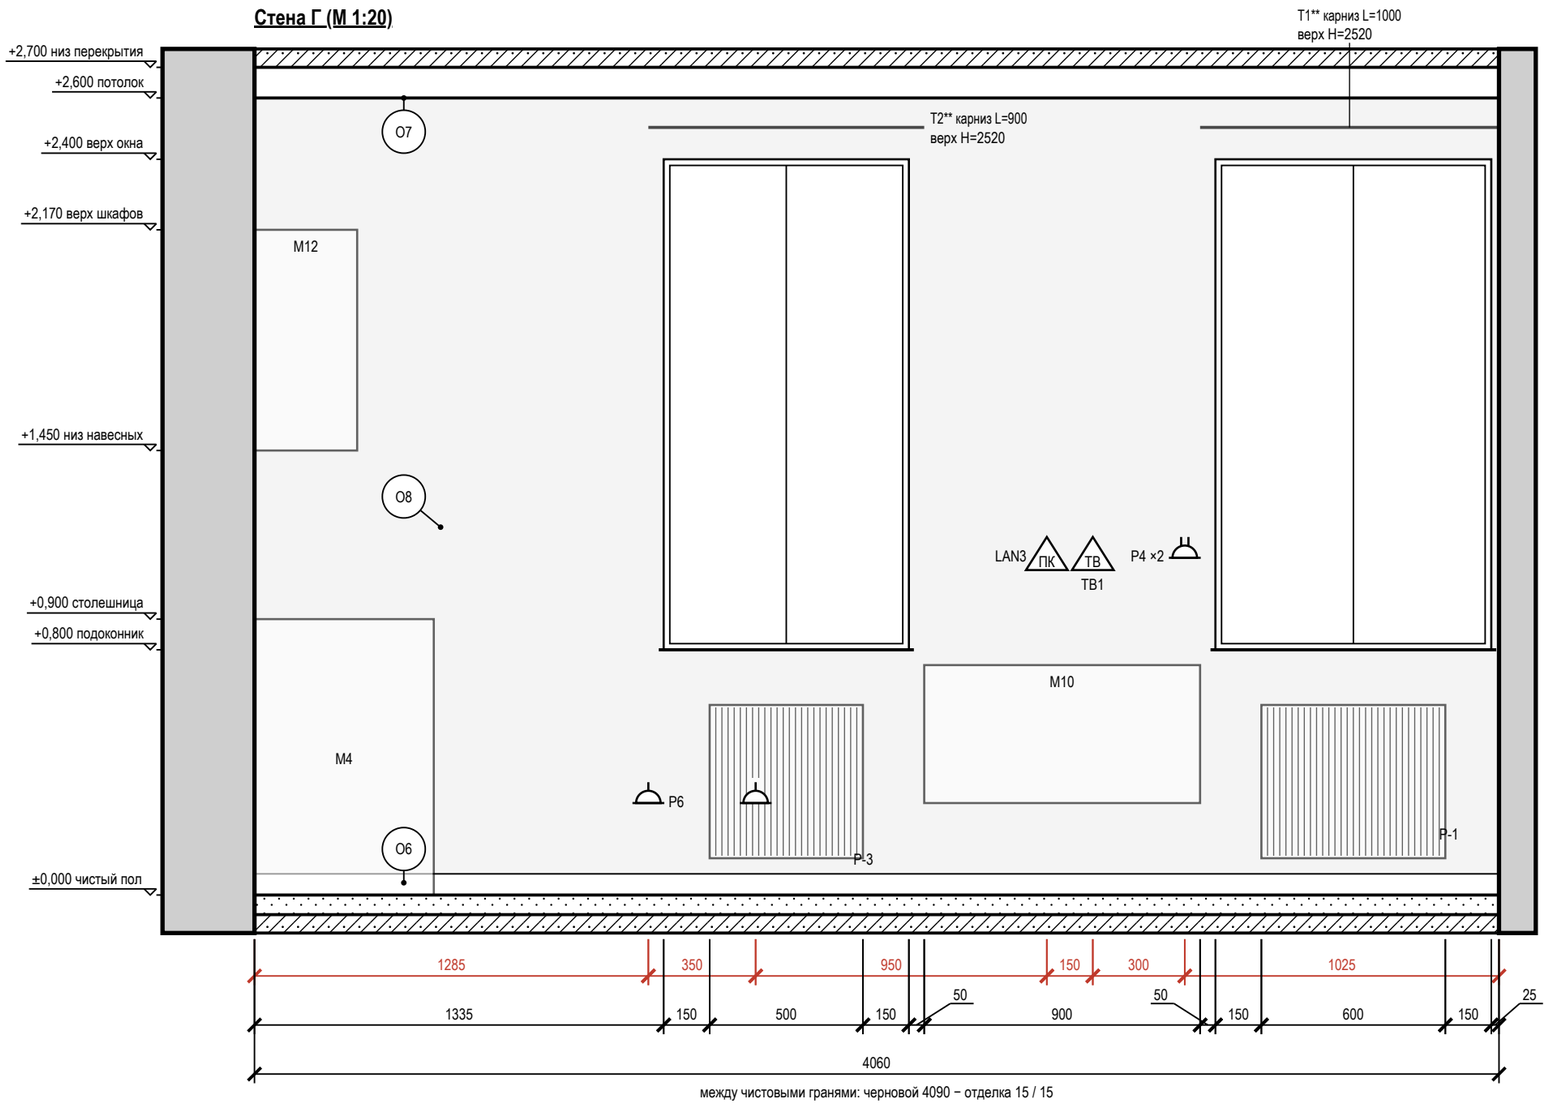

между чистовыми гранями: черновой 4090 − отделка 15 / 15

Ведомость точек и выводов

Марка	Что это	Гр.	H, мм	От угла, мм	Примечание
P6	розетка: торшер у кресла M3**	4	300	1285	
P5	розетка: обеденная зона	4	300	1635	
LAN3	розетка RJ45: Smart TV		1100	2585	
TB1	розетка ТВ: ТВ на стене		1100	2735	
P4	розетка: ТВ, приставка	4	1100	3035	рамка 2 поста

Условные обозначения

- розетка с заземляющим контактом; у знака — марка, ×N постов в рамке, гр. — группа щита, H — высота оси, мм
- ПК — розетка компьютерная RJ45
- ТВ — розетка телевизионная
- привязки точек и выводов от угла и от пола, мм
- мебель и приборы — фасад по расстановке (условно)
- карниз (шина) и шторы в собранном виде: марка T, длина L, верх H
- окно: проём, рама, подоконник
- радиатор отопления; марка — по плану отопления
- стены и перекрытия в сечении
- O1 — марка отделки по реестру отделки альбома
- A — марка развёртки: буква стены, стрелка — взгляд

Ведомость отделки (на листе)

Марка	Поверхность	Материал, изделие	Цвет, код	Кол.
O6	плинтус	плинтус МДФ, Orac Decor Contour (Luxxus), h 69 мм, SX165, шелковисто-матовая	NCS S 0300-N	4,1 м
O7	потолок	окраска, Tikkurila, глубокоматовая	NCS S 0300-N	18,9 м²
O8	стены	окраска, Tikkurila, шелковисто-матовая, подготовка Q3	NCS S 1002-Y50R	7,8 м²

Примечания

1. Развёртки — вид на стену изнутри помещения, по часовой стрелке; расположение — на листе 80; размеры — в мм по чистовым поверхностям; отметки — в м от ±0,000; высоты H — от чистого пола помещения до оси изделия, у декора — до центра.
2. Красная цепочка — привязки электроточек и выводов по осям от угла чистовых стен; высота H — у знака, от чистого пола до оси; высоты мебели, проёмов и границ отделки — колонкой отметок слева. У знака — короткая марка; назначение, группа щита, высота и привязка каждой точки и вывода — в «Ведомости точек и выводов» под видами (каждая точка — строка).
3. У знака электроточки: марка (P — розетка, S — выключатель, Св — светильник, ЭВ — вывод кабеля), ×N — число постов в рамке, гр. — группа щита, H — высота оси от чистого пола, мм; группы по клавишам выключателя — на листе выключателей.
4. Схема мебели, приборов и декора не является технической документацией для производства мебели; габариты — по паспортам изделий.
5. Карнизы (шины) — по ведомости текстиля декоратора: длина L и верх H на развёртке — те же числа, что в ведомости; крепление — до окраски потолка.
6. Выводы кухонной техники — по утверждённому проекту кухни: привязки выводов даются от осей модулей гарнитура.
7. Карниз T1**: по ведомости текстиля шина L=1000 мм, а от её начала до чистового угла стены — 975 мм: шина не встаёт, длину согласовать с декоратором до заказа.
8. Линии узора (швы плитки, складки штор, рёбра радиаторов) прерываются у знаков и выносок — просвет между линиями не менее 0,7 мм.
9. Часть марок не уместилась у знаков: коды, высоты и привязки этих позиций — в ведомости точек и выводов под видами.

Допущения и предложения на листе

Основа листа: размеры сняты с растрового плана заказчика без размеров: масштаб восстановлен по площадям помещений (≈ 11,8 мм на пиксель), контрольный обмер не выполнен (К-1); высота потолка 2700 мм принята: на плане заказчика её нет (К-2); толщины стен 300 / 120 мм приняты по плану заказчика, не замерены (К-1); разрешённая мощность 15 кВт принята по типовым ТУ для квартиры, ТУ заказчиком не переданы (К-4); подрайон климата не задан — принят не северный (жилые от 2,5 м) (К-9).

Знак «**» — предложение проектировщика, заказчиком не утверждено (согласовать с заказчиком): ИЗ-4: T1, T2; К-5: M3 — Было x 800, y 1750 — место занял диван M1.

См. лист открытых вопросов (лист 6, записи К-1, К-2, К-4, К-5; лист 7, запись К-9; лист 8, запись ИЗ-4).

1000 мм · печать 1:1

Изм.	Кол.уч	Лист	№ док.	Подп.	Дата
Разраб.		Кырлан А.С.			14.11.26
Пров.					
ГИП					
Н. контр.					
Утв.					

ГД-2026-007-АИ

Квартира 65 м²

Общая площадь 65,24* м² · * размеры со скана, не замерены (реестр — л. 6–8, К-1)

Дизайн-проект интерьера	Стадия	Лист	Листов
	РП	87	117

Развёртка стены Г. Кухня-гостиная (пом. 3), кухонный фронт

М 1:20

Кырлан Александр Сергеевич


выпуск 14.11.2026 № 9cc0b98f36 · стр. 96 из 139

Развёртки стен А1, А2. Кухня-гостиная (пом. 3)

Кухня-гостиная (пом. 3) · вид изнутри помещения · размеры в мм, отметки в м


ПРЕДВАРИТЕЛЬНО · не для производства работ · открыто пунктов: 14 (реестр — л. 6–8)

Стена А1 (М 1:25)

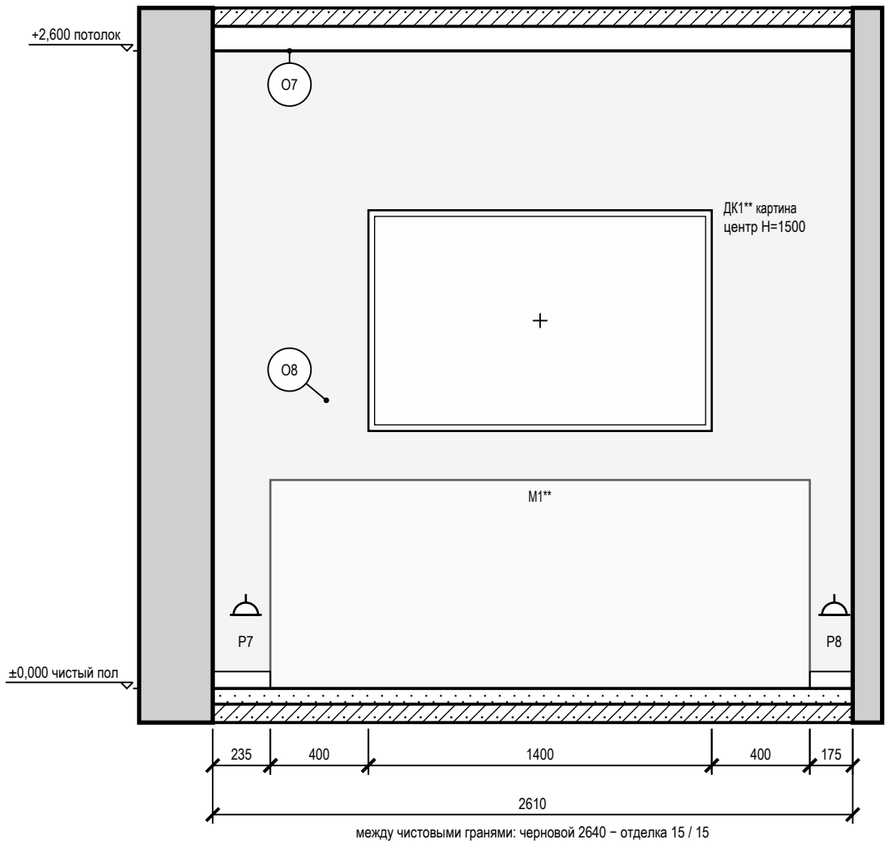

между чистовыми гранями: черновой 2640 − отделка 15 / 15

Стена А2 (М 1:25)

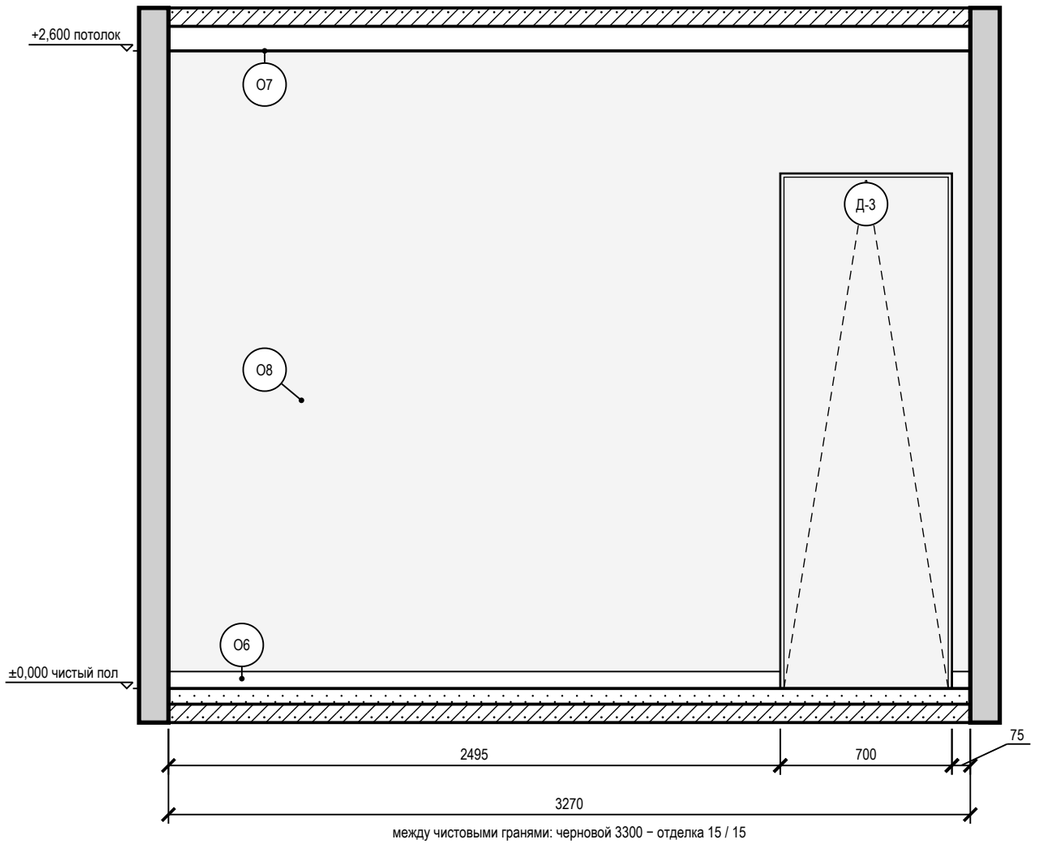

между чистовыми гранями: черновой 3300 − отделка 15 / 15


Ведомость точек и выводов

Стена	Марка	Что это	Гр.	Н, мм	От угла, мм	Примечание
А1	Р7	розетка: у дивана	4	300	135	
А1	Р8	розетка: у дивана	4	300	2535	

Условные обозначения

- розетка с заземляющим контактом; у знака — марка, ×N постов в рамке, гр. — группа щита, Н — высота оси, мм
- привязки точек и выводов от угла и от пола, мм
- мебель и приборы — фасад по расстановке (условно)
- картина (декор): марка Д, крест — центр, Н — высота центра, мм
- дверь скрытого монтажа: полотно в плоскости стены (узел — на листе узлов)
- стены и перекрытия в сечении
- О1 — марка отделки по реестру отделки альбома
- А — марка развёртки: буква стены, стрелка — взгляд

Схема развёрток (М 1:200)

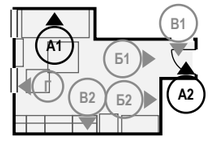

Примечания

1. Развёртки — вид на стену изнутри помещения, по часовой стрелке; расположение — на схеме листа и на листе 80; размеры — в мм по чистовым поверхностям; отметки — в м от ±0,000; высоты Н — от чистого пола помещения до оси изделия, у декора — до центра.
2. Красная цепочка — привязки электроточек и выводов по осям от угла чистовых стен; высота Н — у знака, от чистого пола до оси; высоты мебели, проёмов и границ отделки — колонкой отметок слева. У знака — короткая марка; назначение, группа щита, высота и привязка каждой точки и вывода — в «Ведомости точек и выводов» под видами (каждая точка — строка).
3. Отделка стен — по ведомости отделки помещений, лист 57.
4. У знака электроточки: марка (Р — розетка, S — выключатель, Св — светильник, ЭВ — вывод кабеля), ×N — число постов в рамке, гр. — группа щита, Н — высота оси от чистого пола, мм; группы по клавишам выключателя — на листе выключателей.
5. Схема мебели, приборов и декора не является технической документацией для производства мебели; габариты — по паспортам изделий.
6. Картины и зеркала крепить к основанию по паспорту изделия (закладные и анкеры — в перечне скрытых работ); крест — ось центра предмета.
7. Двери скрытого монтажа — полотно в плоскости стены, отделка стены по полотну, плинтус прерывается у короба (узел — на листе узлов).

Допущения и предложения на листе. Основа листа: размеры сняты с растрового плана заказчика без размеров: масштаб восстановлен по площадям помещений (≈ 11,8 мм на пиксель), контрольный обмер не выполнен (К-1); высота потолка 2700 мм принята: на плане заказчика её нет (К-2); толщины стен 300 / 120 мм приняты по плану заказчика, не замерены (К-1); разрешённая мощность 15 кВт принята по типовым ТУ для квартиры, ТУ заказчиком не переданы (К-4); подрайон климата не задан — принят не северный (жилые от 2,5 м) (К-9). Знак «**» — предложение проектировщика, заказчиком не утверждено (согласовать с заказчиком): К-5: М1 — Было х 2900, у 3000 — в полосе 1400 мм между спальней и кухней, единственном проходе от двери Д-2: стыки частей 290 / 200 / 0 мм (→). См. лист открытых вопросов (лист 6, записи К-1, К-2, К-4, К-5; лист 7, запись К-9; лист 8, запись ИЗ-4).

1000 мм · печать 1:1

Изм.	Кол.уч	Лист	№ док.	Подп.	Дата
Разраб.		Кырлан А.С.			14.11.26
Пров.					
ГИП					
Н. контр.					
Утв.					

ГД-2026-007-АИ

Квартира 65 м²

Общая площадь 65,24* м² · * размеры со скана, не замерены (реестр — л. 6–8, К-1)

Дизайн-проект интерьера

Стадия	Лист	Листов
РП	88	117

Развёртки стен А1, А2. Кухня-гостиная (пом. 3)

М 1:25

Кырлан Александр Сергеевич


выпуск 14.11.2026 № 9cc0b98f36 · стр. 97 из 139

Развёртки стен Б1, Б2, В1. Кухня-гостиная (пом. 3)

Кухня-гостиная (пом. 3) · вид изнутри помещения · размеры в мм, отметки в м


ПРЕДВАРИТЕЛЬНО · не для производства работ · открыто пунктов: 14 (реестр — л. 6–8)

Стена Б1 (М 1:25)

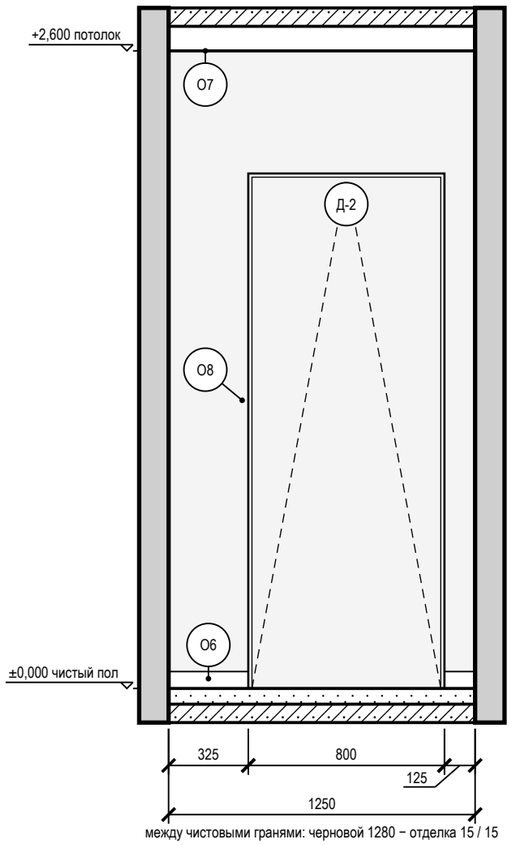


между чистовыми гранями: черновой 1280 − отделка 15 / 15

Стена Б2 (М 1:25)

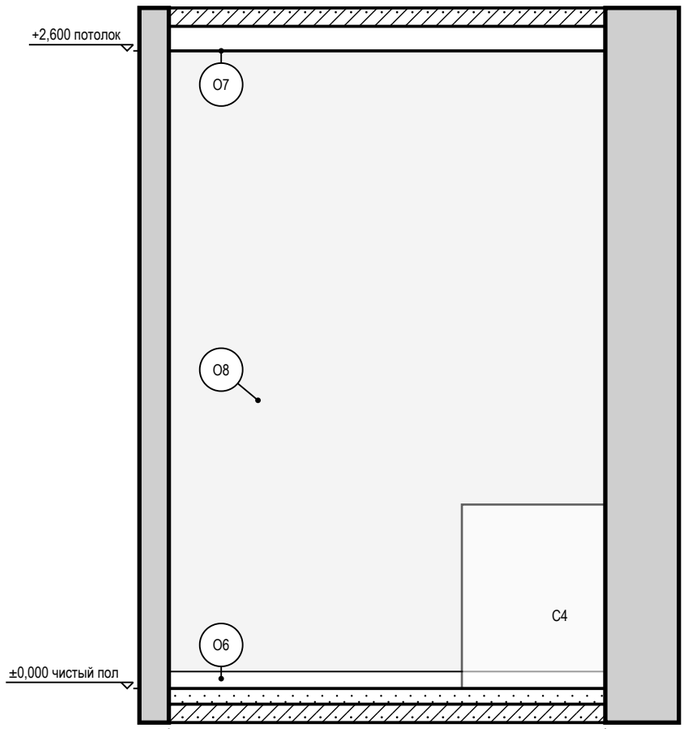

между чистовыми гранями: черновой 1810 − отделка 15 / 15

Стена В1 (М 1:25)

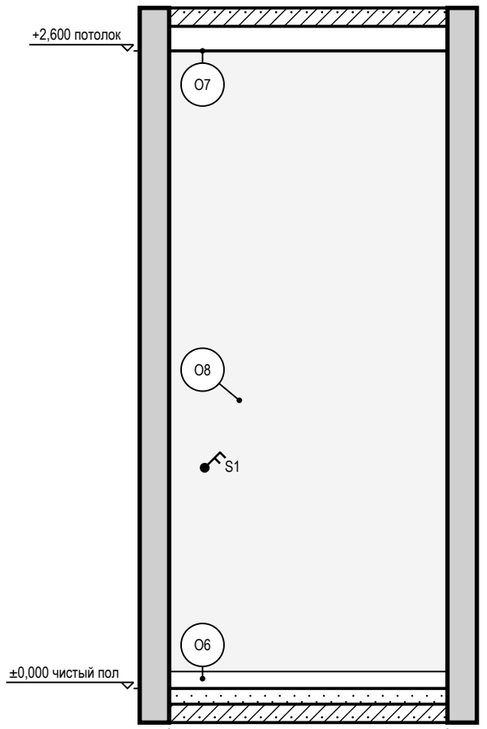


между чистовыми гранями: черновой 1150 − отделка 15 / 0

Условные обозначения

- выключатель одноклавишный
- выключатель двухклавишный (флажков — по числу клавиш)
- привязки точек и выводов от угла и от пола, мм
- мебель и приборы — фасад по расстановке (условно)
- дверь скрытого монтажа: полотно в плоскости стены (узел — на листе узлов)
- стены и перекрытия в сечении
- О1 — марка отделки по реестру отделки альбома
- А — марка развёртки: буква стены, стрелка — взгляд

Схема развёрток (М 1:100)

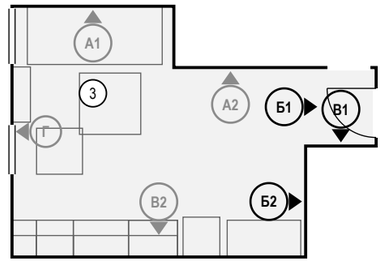

Ведомость точек и выводов

Стена	Марка	Что это	Гр.	Н, мм	От угла, мм	Примечание
В1	S1	выключатель	1	900	145	

Ведомость отделки (на листе)

Марка	Поверхность	Материал, изделие	Цвет, код	Кол.
О6	плинтус	плинтус МДФ, Orac Decor Contour (Luxxus), h 69 мм, SX165, шелковисто-матовая	NCS S 0300-N	3,4 м
О7	потолок	окраска, Tikkurila, глубокоматовая	NCS S 0300-N	18,9 м²
О8	стены	окраска, Tikkurila, шелковисто-матовая, подготовка Q3	NCS S 1002-Y50R	9,1 м²

Примечания

1. Развёртки — вид на стену изнутри помещения, по часовой стрелке; расположение — на схеме листа и на листе 80; размеры — в мм по чистовым поверхностям; отметки — в м от ±0,000; высоты Н — от чистого пола помещения до оси изделия, у декора — до центра.
2. Красная цепочка — привязки электроточек и выводов по осям от угла чистовых стен; высота Н — у знака, от чистого пола до оси; высоты мебели, проёмов и границ отделки — колонкой отметок слева. У знака — короткая марка; назначение, группа щита, высота и привязка каждой точки и вывода — в «Ведомости точек и выводов» под видами (каждая точка — строка).
3. У знака электроточки: марка (Р — розетка, S — выключатель, Св — светильник, ЭВ — вывод кабеля), ×N — число постов в рамке, гр. — группа щита, Н — высота оси от чистого пола, мм; группы по клавишам выключателя — на листе выключателей.
4. Схема мебели, приборов и декора не является технической документацией для производства мебели; габариты — по паспортам изделий.
5. Двери скрытого монтажа — полотно в плоскости стены, отделка стены по полотну, плинтус прерывается у короба (узел — на листе узлов).

Допущения и предложения на листе

Основа листа: размеры сняты с растрового плана заказчика без размеров: масштаб восстановлен по площадям помещений (≈ 11,8 мм на пиксель), контрольный обмер не выполнен (К-1); высота потолка 2700 мм принята: на плане заказчика её нет (К-2); толщины стен 300 / 120 мм приняты по плану заказчика, не замерены (К-1); разрешённая мощность 15 кВт принята по типовым ТУ для квартиры, ТУ заказчиком не переданы (К-4); подрайон климата не задан — принят не северный (жилые от 2,5 м) (К-9).
См. лист открытых вопросов (лист 6, записи К-1, К-2, К-4; лист 7, запись К-9).

1000 мм · печать 1:1

Изм.	Кол.уч	Лист	№ док.	Подп.	Дата
Разраб.		Кырлан А.С.			14.11.26
Пров.					
ГИП					
Н. контр.					
Утв.					

ГД-2026-007-АИ

Квартира 65 м²

Общая площадь 65,24* м² · * размеры со скана, не замерены (реестр — л. 6–8, К-1)

Дизайн-проект интерьера

Стадия	Лист	Листов
РП	89	117

Развёртки стен Б1, Б2, В1. Кухня-гостиная (пом. 3)
М 1:25

Кырлан Александр Сергеевич


выпуск 14.11.2026 № 9cc0b98f36 · стр. 98 из 139

Развёртки стен А, Б. Прихожая (пом. 4)

Прихожая (пом. 4) · вид изнутри помещения · размеры в мм, отметки в м


ПРЕДВАРИТЕЛЬНО · не для производства работ · открыто пунктов: 14 (реестр — л. 6–8)

Стена А (М 1:25)

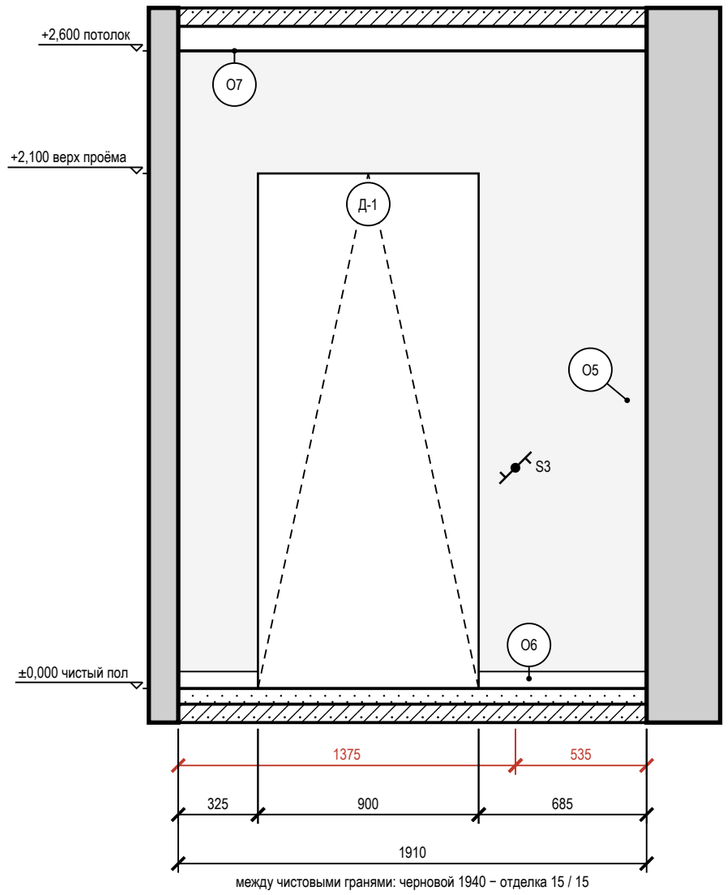

между чистовыми гранями: черновой 1940 − отделка 15 / 15

Стена Б (М 1:25)

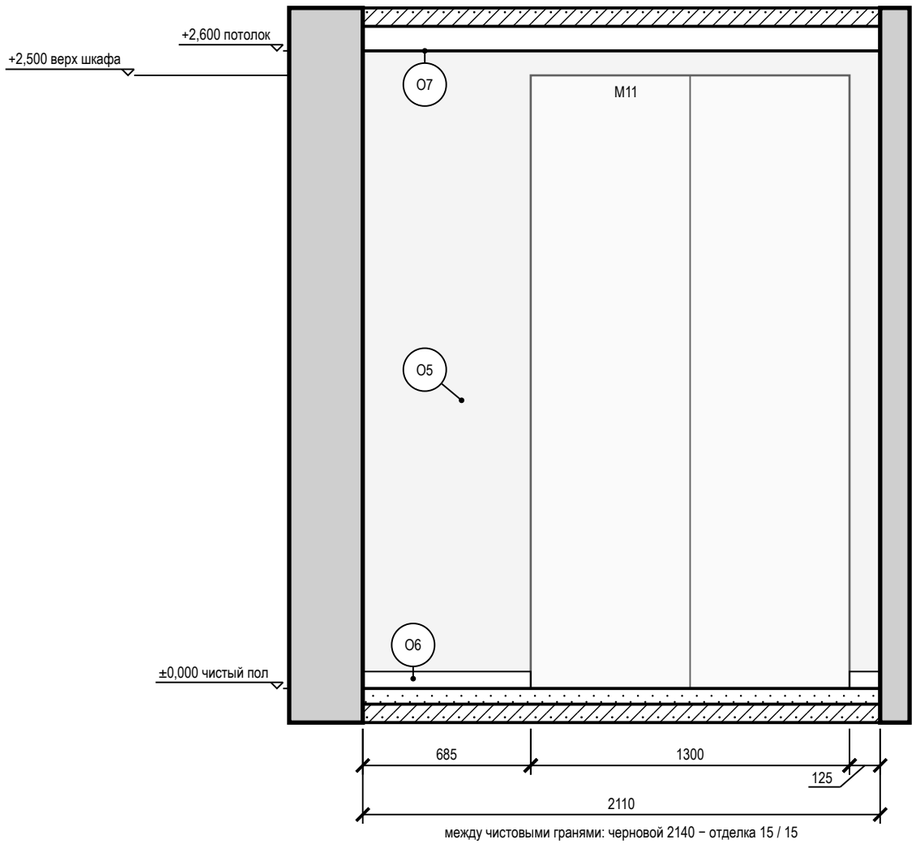


между чистовыми гранями: черновой 2140 − отделка 15 / 15

Условные обозначения

- выключатель одноклавишный
- выключатель с проходной или перекрёстной клавишей (обратный флажок); тип клавиши — в подписи
- привязки точек и выводов от угла и от пола, мм
- мебель и приборы — фасад по расстановке (условно)
- дверной проём; марка двери — в кружке
- стены и перекрытия в сечении
- О1 — марка отделки по реестру отделки альбома
- А — марка развёртки: буква стены, стрелка — взгляд

Схема развёрток (М 1:50)

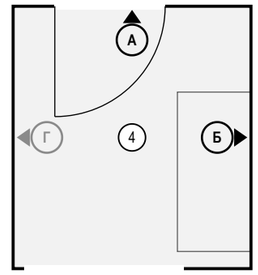

Ведомость точек и выводов

Стена	Марка	Что это	Гр.	Н, мм	От угла, мм	Примечание
А	S3	выключатель	1	900	1375	

Ведомость отделки (на листе)

Марка	Поверхность	Материал, изделие	Цвет, код	Кол.
О5	стены	окраска, Tikkurila, шелковисто-матовая, подготовка Q3	NCS S 1502-Y50R	8,6 м²
О6	плинтус	плинтус МДФ, Orac Decor Contour (Luxxus), h 69 мм, SX165, шелковисто-матовая	NCS S 0300-N	1,8 м
О7	потолок	окраска, Tikkurila, глубокоматовая	NCS S 0300-N	4,2 м²

Примечания

1. Развёртки — вид на стену изнутри помещения, по часовой стрелке; расположение — на схеме листа и на листе 80; размеры — в мм по чистовым поверхностям; отметки — в м от ±0,000; высоты Н — от чистого пола помещения до оси изделия, у декора — до центра.
2. Красная цепочка — привязки электроточек и выводов по осям от угла чистовых стен; высота Н — у знака, от чистого пола до оси; высоты мебели, проёмов и границ отделки — колонкой отметок слева. У знака — короткая марка; назначение, группа щита, высота и привязка каждой точки и вывода — в «Ведомости точек и выводов» под видами (каждая точка — строка).
3. У знака электроточки: марка (Р — розетка, S — выключатель, Св — светильник, ЭВ — вывод кабеля), ×N — число постов в рамке, гр. — группа щита, Н — высота оси от чистого пола, мм; группы по клавишам выключателя — на листе выключателей.
4. Схема мебели, приборов и декора не является технической документацией для производства мебели; габариты — по паспортам изделий.

Допущения и предложения на листе

Основа листа: размеры сняты с растрового плана заказчика без размеров: масштаб восстановлен по площадям помещений (≈ 11,8 мм на пиксель), контрольный обмер не выполнен (К-1); высота потолка 2700 мм принята: на плане заказчика её нет (К-2); толщины стен 300 / 120 мм приняты по плану заказчика, не замерены (К-1); разрешённая мощность 15 кВт принята по типовым ТУ для квартиры, ТУ заказчиком не переданы (К-4); подрайон климата не задан — принят не северный (жилые от 2,5 м) (К-9).
См. лист открытых вопросов (лист 6, записи К-1, К-2, К-4; лист 7, запись К-9).

1000 мм · печать 1:1

Изм.	Кол.уч	Лист	№ док.	Подп.	Дата
Разраб.		Кырлан А.С.			14.11.26
Пров.					
ГИП					
Н. контр.					
Утв.					

ГД-2026-007-АИ

Квартира 65 м²

Общая площадь 65,24* м² · * размеры со скана, не замерены (реестр — л. 6–8, К-1)

Дизайн-проект интерьера

Стадия	Лист	Листов
РП	90	117

Развёртки стен А, Б. Прихожая (пом. 4)

М 1:25

Кырлан Александр Сергеевич


выпуск 14.11.2026 № 9cc0b98f36 · стр. 99 из 139

Развёртка стены Г. Прихожая (пом. 4)

Прихожая (пом. 4) · вид изнутри помещения · размеры в мм, отметки в м

ПРЕДВАРИТЕЛЬНО · не для производства работ · открыто пунктов: 14 (реестр — л. 6–8)

Стена Г (М 1:20)

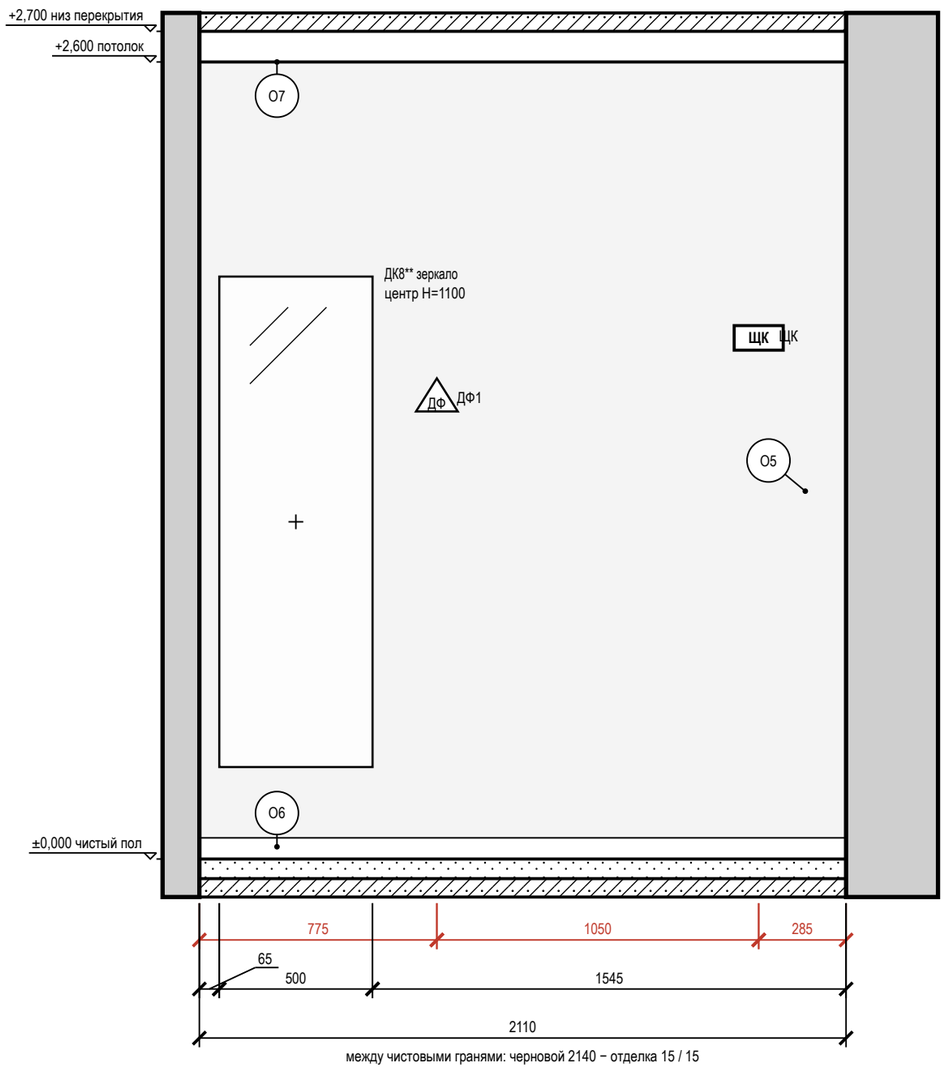

между чистовыми гранями: черновой 2140 − отделка 15 / 15

Ведомость точек и выводов

Марка	Что это	Гр.	Н, мм	От угла, мм	Примечание
ДФ1	домофон: трубка домофона		1500	775	
ЩК	щит		1700	1825	


Условные обозначения

- ДФ — трубка или монитор домофона
- ЩК — щит квартирный
- привязки точек и выводов от угла и от пола, мм
- мебель и приборы — фасад по расстановке (условно)
- зеркало: марка Д, крест — центр, Н — высота центра, мм
- стены и перекрытия в сечении
- О1 — марка отделки по реестру отделки альбома
- А — марка развёртки: буква стены, стрелка — взгляд

Ведомость отделки (на листе)

Марка	Поверхность	Материал, изделие	Цвет, код	Кол.
О5	стены	окраска, Tikkurila, шелковисто-матовая, подготовка Q3	NCS S 1502-Y50R	5,5 м²
О6	плинтус	плинтус МДФ, Orac Decor Contour (Luxxus), h 69 мм, SX165, шелковисто-матовая	NCS S 0300-N	2,1 м
О7	потолок	окраска, Tikkurila, глубокоматовая	NCS S 0300-N	4,2 м²

Схема развёрток (М 1:50)

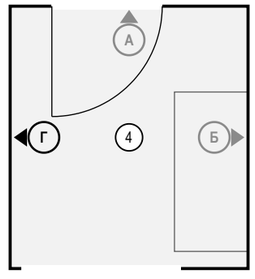

Ведомость изделий и проёмов (на листе)

Марка	Изделие, проём	На виде Ш×В, мм	Низ, мм
ДК8**	зеркало	500×1600	300

Примечания

1. Развёртки — вид на стену изнутри помещения, по часовой стрелке; расположение — на схеме листа и на листе 80; размеры — в мм по чистовым поверхностям; отметки — в м от ±0,000; высоты Н — от чистого пола помещения до оси изделия, у декора — до центра.
2. Красная цепочка — привязки электроточек и выводов по осям от угла чистовых стен; высота Н — у знака, от чистого пола до оси; высоты мебели, проёмов и границ отделки — колонкой отметок слева. У знака — короткая марка; назначение, группа щита, высота и привязка каждой точки и вывода — в «Ведомости точек и выводов» под видами (каждая точка — строка).
3. У знака электроточки: марка (Р — розетка, S — выключатель, Св — светильник, ЭВ — вывод кабеля), ×N — число постов в рамке, гр. — группа щита, Н — высота оси от чистого пола, мм; группы по клавишам выключателя — на листе выключателей.
4. Схема мебели, приборов и декора не является технической документацией для производства мебели; габариты — по паспортам изделий.
5. Картины и зеркала крепить к основанию по паспорту изделия (закладные и анкеры — в перечне скрытых работ); крест — ось центра предмета.

Допущения и предложения на листе

Основа листа: размеры сняты с растрового плана заказчика без размеров: масштаб восстановлен по площадям помещений (≈ 11,8 мм на пиксель), контрольный обмер не выполнен (К-1); высота потолка 2700 мм принята: на плане заказчика её нет (К-2); толщины стен 300 / 120 мм приняты по плану заказчика, не замерены (К-1); разрешённая мощность 15 кВт принята по типовым ТУ для квартиры, ТУ заказчиком не переданы (К-4); подрайон климата не задан — принят не северный (жилые от 2,5 м) (К-9).
Знак «**» — предложение проектировщика, заказчиком не утверждено (согласовать с заказчиком): ИЗ-4: ДК8.
См. лист открытых вопросов (лист 6, записи К-1, К-2, К-4; лист 7, запись К-9; лист 8, запись ИЗ-4).

1000 мм · печать 1:1

Изм.	Кол.уч	Лист	№ док.	Подп.	Дата
Разраб.		Кырлан А.С.			14.11.26
Пров.					
ГИП					
Н. контр.					
Утв.					

ГД-2026-007-АИ

Квартира 65 м²

Общая площадь 65,24* м² · * размеры со скана, не замерены (реестр — л. 6–8, К-1)

Дизайн-проект интерьера

Стадия	Лист	Листов
РП	91	117

Развёртка стены Г. Прихожая (пом. 4)

М 1:20

Кырлан Александр Сергеевич


выпуск 14.11.2026 № 9cc0b98f36 · стр. 100 из 139

Развёртки стен А, Б. Коридор (пом. 5)

Коридор (пом. 5) · вид изнутри помещения · размеры в мм, отметки в м


ПРЕДВАРИТЕЛЬНО · не для производства работ · открыто пунктов: 14 (реестр — л. 6–8)

Стена А (М 1:25)

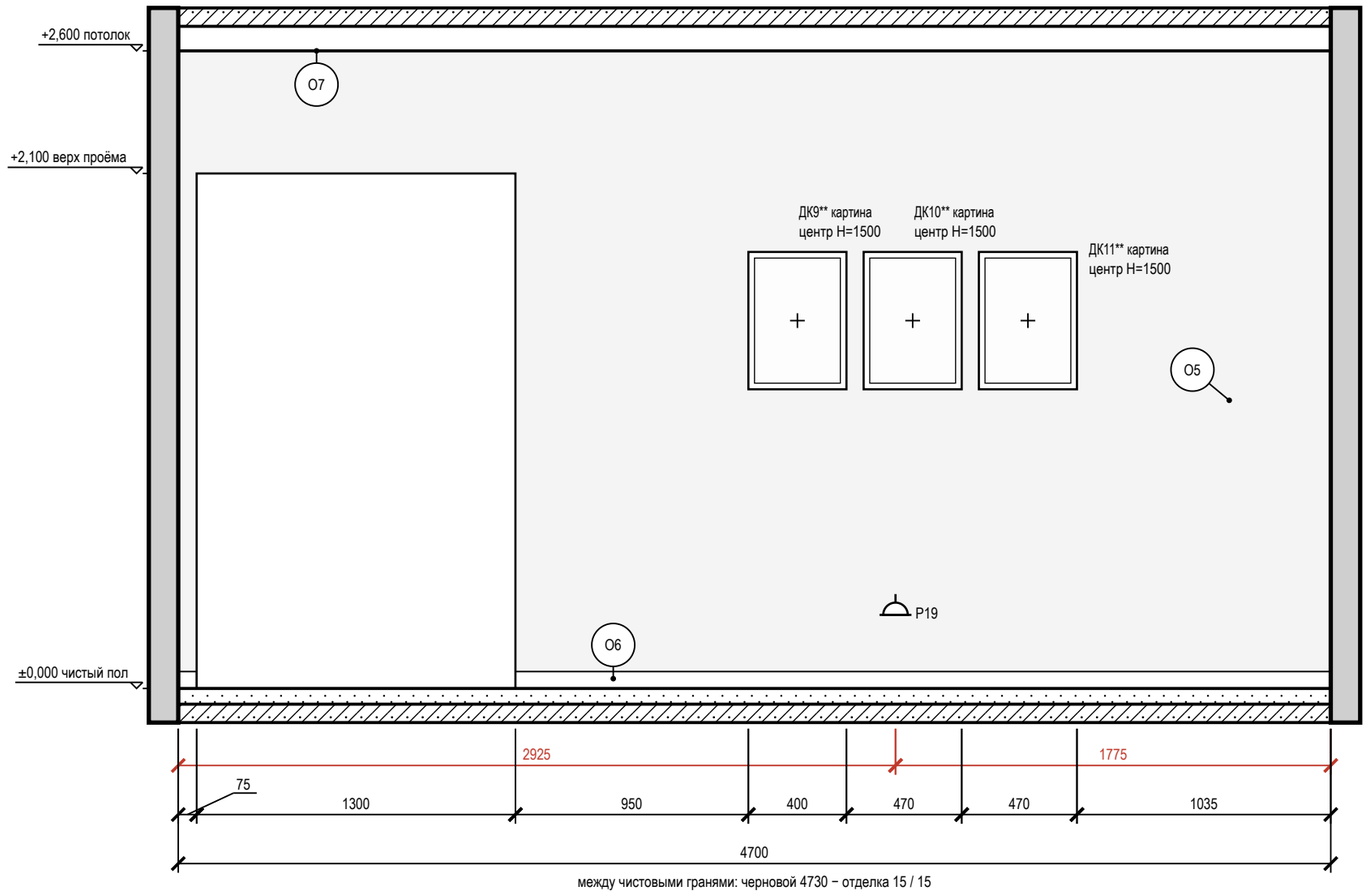

между чистовыми гранями: черновой 4730 − отделка 15 / 15

Стена Б (М 1:25)

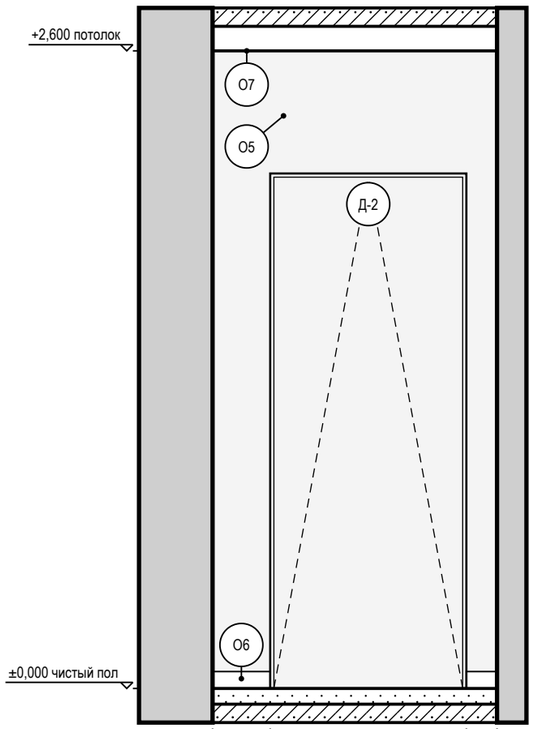

между чистовыми гранями: черновой 1190 − отделка 15 / 15

Ведомость точек и выводов

Стена	Марка	Что это	Гр.	H, мм	От угла, мм	Примечание
А	Р19	розетка: уборка	4	300	2925	

Условные обозначения

- розетка с заземляющим контактом; у знака — марка, ×N постов в рамке, гр. — группа щита, H — высота оси, мм
- привязки точек и выводов от угла и от пола, мм
- мебель и приборы — фасад по расстановке (условно)
- картина (декор): марка Д, крест — центр, H — высота центра, мм
- дверь скрытого монтажа: полотно в плоскости стены (узел — на листе узлов)
- дверной проём; марка двери — в кружке
- стены и перекрытия в сечении
- О1 — марка отделки по реестру отделки альбома
- А — марка развёртки: буква стены, стрелка — взгляд

Допущения и предложения на листе

Основа листа: размеры сняты с растрового плана заказчика без размеров: масштаб восстановлен по площадям помещений (≈ 11,8 мм на пиксель), контрольный обмер не выполнен (К-1); высота потолка 2700 мм принята: на плане заказчика её нет (К-2); толщины стен 300 / 120 мм приняты по плану заказчика, не замерены (К-1); разрешённая мощность 15 кВт принята по типовым ТУ для квартиры, ТУ заказчиком не переданы (К-4); подрайон климата не задан — принят не северный (жилые от 2,5 м) (К-9).
Знак «**» — предложение проектировщика, заказчиком не утверждено (согласовать с заказчиком): ИЗ-4: ДК9, ДК10, ДК11.
См. лист открытых вопросов (лист 6, записи К-1, К-2, К-4; лист 7, запись К-9; лист 8, запись ИЗ-4).

Примечания

1. Развёртки — вид на стену изнутри помещения, по часовой стрелке; расположение — на листе 80; размеры — в мм по чистовым поверхностям; отметки — в м от ±0,000; высоты H — от чистого пола помещения до оси изделия, у декора — до центра.
2. Красная цепочка — привязки электроточек и выводов по осям от угла чистовых стен; высота H — у знака, от чистого пола до оси; высоты мебели, проёмов и границ отделки — колонкой отметок слева. У знака — короткая марка; назначение, группа щита, высота и привязка каждой точки и вывода — в «Ведомости точек и выводов» под видами (каждая точка — строка).
3. Отделка стен — по ведомости отделки помещений, лист 57.
4. У знака электроточки: марка (Р — розетка, S — выключатель, Св — светильник, ЭВ — вывод кабеля), ×N — число постов в рамке, гр. — группа щита, H — высота оси от чистого пола, мм; группы по клавишам выключателя — на листе выключателей.
5. Схема мебели, приборов и декора не является технической документацией для производства мебели; габариты — по паспортам изделий.
6. Картины и зеркала крепить к основанию по паспорту изделия (закладные и анкеры — в перечне скрытых работ); крест — ось центра предмета.
7. Двери скрытого монтажа — полотно в плоскости стены, отделка стены по полотну, плинтус прерывается у короба (узел — на листе узлов).

1000 мм · печать 1:1

Изм.	Кол.уч	Лист	№ док.	Подп.	Дата
Разраб.		Кырлан А.С.			14.11.26
Пров.					
ГИП					
Н. контр.					
Утв.					

ГД-2026-007-АИ

Квартира 65 м²

Общая площадь 65,24* м² · * размеры со скана, не замерены (реестр — л. 6–8, К-1)

Дизайн-проект интерьера

Стадия	Лист	Листов
РП	92	117

Развёртки стен А, Б. Коридор (пом. 5)

М 1:25

Кырлан Александр Сергеевич


выпуск 14.11.2026 № 9cc0b98f36 · стр. 101 из 139

Развёртки стен В, Г. Коридор (пом. 5)

Коридор (пом. 5) · вид изнутри помещения · размеры в мм, отметки в м


ПРЕДВАРИТЕЛЬНО · не для производства работ · открыто пунктов: 14 (реестр — л. 6–8)

Стена В (М 1:25)

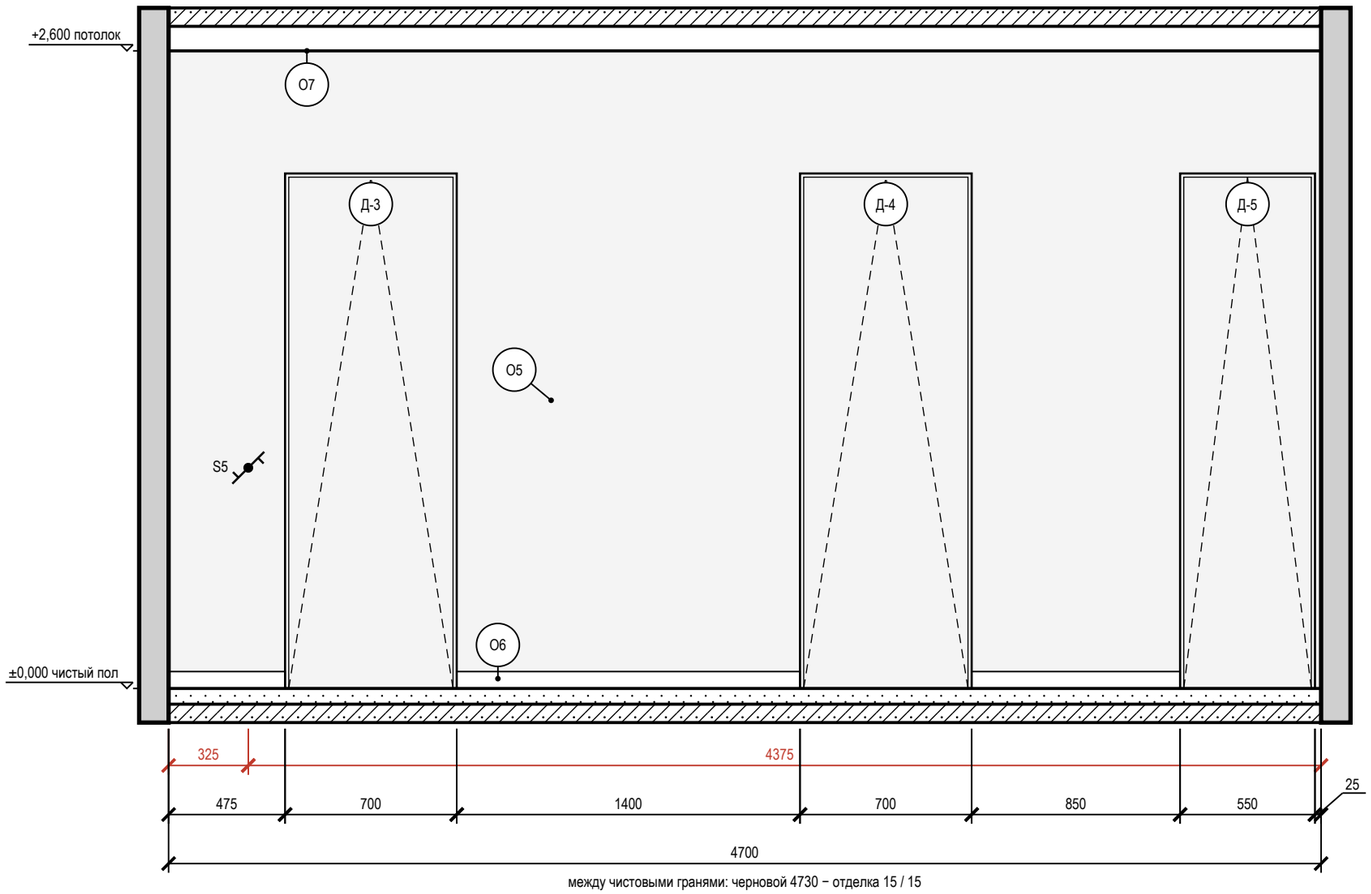

между чистовыми гранями: черновой 4730 − отделка 15 / 15

Стена Г (М 1:25)

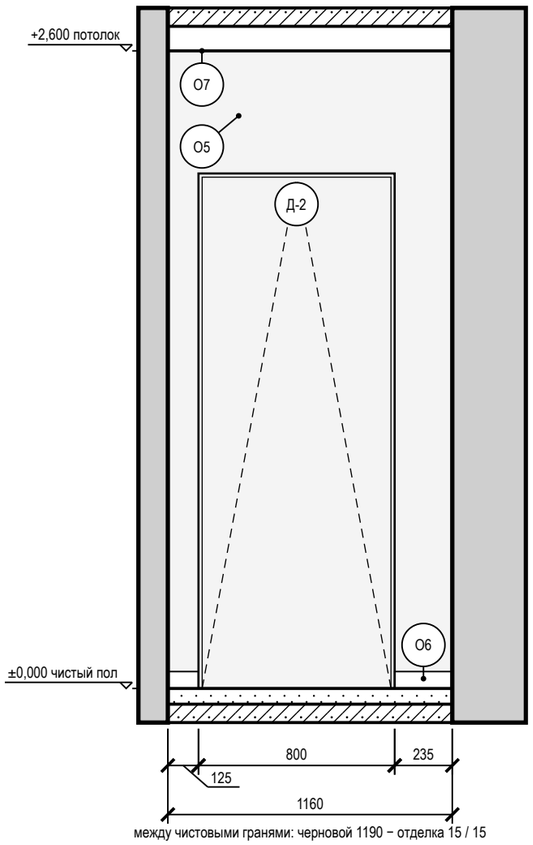

между чистовыми гранями: черновой 1190 − отделка 15 / 15

Ведомость точек и выводов

Стена	Марка	Что это	Гр.	H, мм	От угла, мм	Примечание
В	S5	выключатель	1	900	325	

Условные обозначения

- выключатель одноклавишный
- выключатель с проходной или перекрёстной клавишей (обратный флажок); тип клавиши — в подписи
- привязки точек и выводов от угла и от пола, мм
- мебель и приборы — фасад по расстановке (условно)
- дверь скрытого монтажа: полотно в плоскости стены (узел — на листе узлов)
- стены и перекрытия в сечении
- О1 — марка отделки по реестру отделки альбома
- А — марка развёртки: буква стены, стрелка — взгляд

Примечания

1. Развёртки — вид на стену изнутри помещения, по часовой стрелке; расположение — на листе 80; размеры — в мм по чистовым поверхностям; отметки — в м от ±0,000; высоты H — от чистого пола помещения до оси изделия, у декора — до центра.
2. Красная цепочка — привязки электроточек и выводов по осям от угла чистовых стен; высота H — у знака, от чистого пола до оси; высоты мебели, проёмов и границ отделки — колонкой отметок слева. У знака — короткая марка; назначение, группа щита, высота и привязка каждой точки и вывода — в «Ведомости точек и выводов» под видами (каждая точка — строка).
3. Отделка стен — по ведомости отделки помещений, лист 57.
4. У знака электроточки: марка (Р — розетка, S — выключатель, Св — светильник, ЭВ — вывод кабеля), ×N — число постов в рамке, гр. — группа щита, H — высота оси от чистого пола, мм; группы по клавишам выключателя — на листе выключателей.
5. Схема мебели, приборов и декора не является технической документацией для производства мебели; габариты — по паспортам изделий.
6. Двери скрытого монтажа — полотно в плоскости стены, отделка стены по полотну, плинтус прерывается у короба (узел — на листе узлов).

Допущения и предложения на листе

Основа листа: размеры сняты с растрового плана заказчика без размеров: масштаб восстановлен по площадям помещений (≈ 11,8 мм на пиксель), контрольный обмер не выполнен (К-1); высота потолка 2700 мм принята: на плане заказчика её нет (К-2); толщины стен 300 / 120 мм приняты по плану заказчика, не замерены (К-1); разрешённая мощность 15 кВт принята по типовым ТУ для квартиры, ТУ заказчиком не переданы (К-4); подрайон климата не задан — принят не северный (жилые от 2,5 м) (К-9).

См. лист открытых вопросов (лист 6, записи К-1, К-2, К-4; лист 7, запись К-9).

1000 мм · печать 1:1

Изм.	Кол.уч	Лист	№ док.	Подп.	Дата
Разраб.		Кырлан А.С.			14.11.26
Пров.					
ГИП					
Н. контр.					
Утв.					

ГД-2026-007-АИ

Квартира 65 м²

Общая площадь 65,24* м² · * размеры со скана, не замерены (реестр — л. 6–8, К-1)

Дизайн-проект интерьера

Стадия	Лист	Листов
РП	93	117

Развёртки стен В, Г. Коридор (пом. 5)

М 1:25

Кырлан Александр Сергеевич


выпуск 14.11.2026 № 9cc0b98f36 · стр. 102 из 139

Развёртки стен А, Б. Санузел (пом. 6)

Санузел (пом. 6) · вид изнутри помещения · размеры в мм, отметки в м


ПРЕДВАРИТЕЛЬНО · не для производства работ · открыто пунктов: 14 (реестр — л. 6–8)

Стена А (М 1:20)

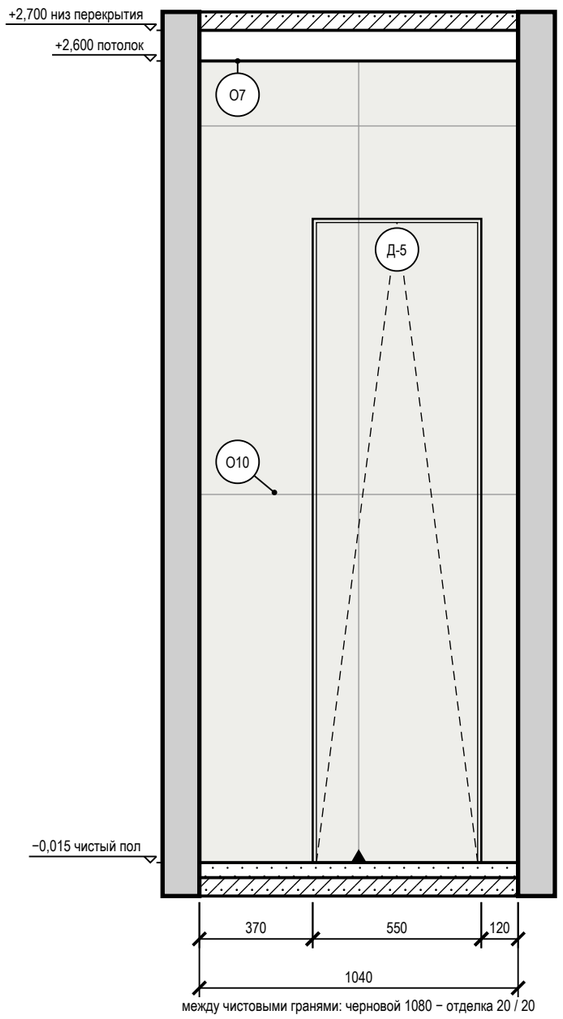

между чистовыми гранями: черновой 1080 − отделка 20 / 20

Стена Б (М 1:20)

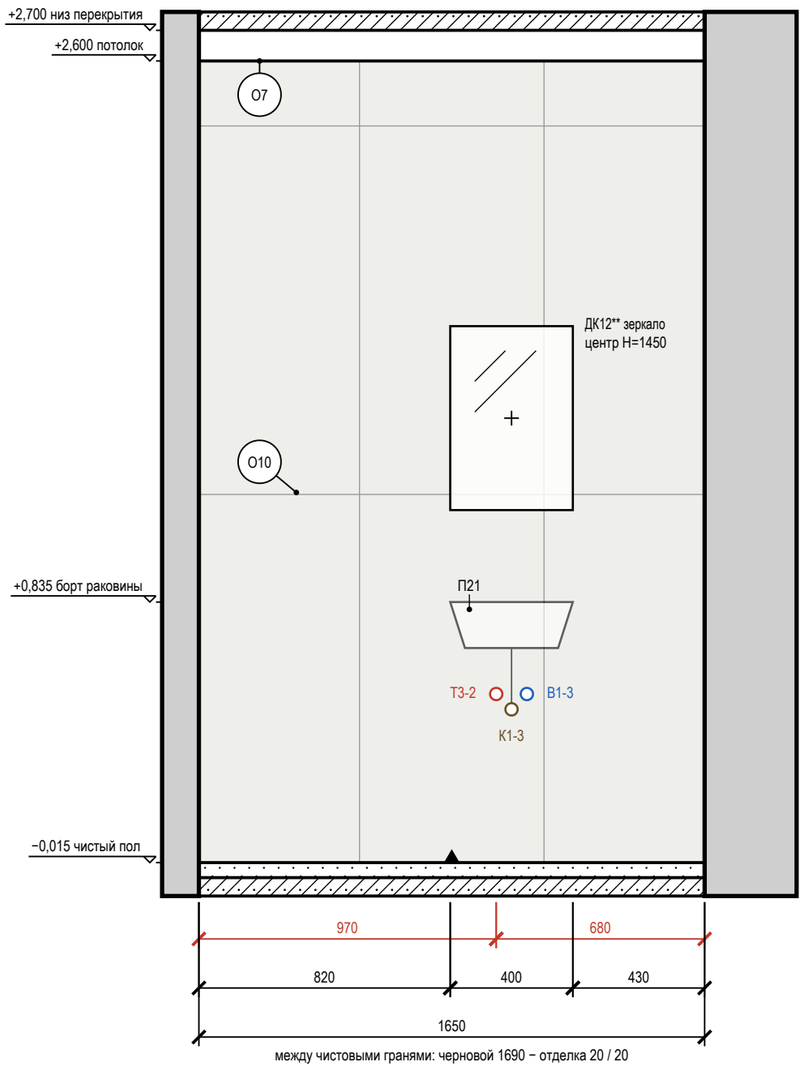

между чистовыми гранями: черновой 1690 − отделка 20 / 20

Ведомость точек и выводов

Стена	Марка	Что это	Гр.	Н, мм	От угла, мм	Примечание
Б	Т3-2	горячая вода — умывальник		550	970	межос. 100
Б	К1-3	канализация — умывальник		500	1020	Ø50
Б	В1-3	холодная вода — умывальник		550	1070	межос. 100


Условные обозначения

- вывод В1 (код — в ведомости привязок)
- вывод Т3 (код — в ведомости привязок)
- вывод К1 (код — в ведомости привязок)
- привязки точек и выводов от угла и от пола, мм
- мебель и приборы — фасад по расстановке (условно)
- зеркало: марка Д, крест — центр, Н — высота центра, мм
- дверь скрытого монтажа: полотно в плоскости стены (узел — на листе узлов)
- стены и перекрытия в сечении
- плитка: сетка швов по формату, ▲ — ось старта
- О1 — марка отделки по реестру отделки альбома
- А — марка развёртки: буква стены, стрелка взгляд

Ведомость отделки (на листе)

Марка	Поверхность	Материал, изделие	Цвет, код	Кол.
О7	потолок	окраска, Tikkurila, глубокоматовая	NCS S 0300-N	1,8 м²
О10	стены	облицовка плиткой, Italon Charme Extra, 600×1200 мм, 610010001195	Italon 610010001195 «Charme Extra»	5,9 м²

Схема развёрток (М 1:50)

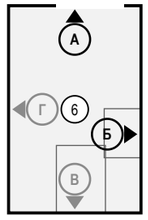

Примечания

1. Развёртки — вид на стену изнутри помещения, по часовой стрелке; расположение — на схеме листа и на листе 80; размеры — в мм по чистовым поверхностям; отметки — в м от ±0,000; высоты Н — от чистого пола помещения до оси изделия, у декора — до центра.
2. Красная цепочка — привязки электроточек и выводов по осям от угла чистовых стен; высота Н — у знака, от чистого пола до оси; высоты мебели, проёмов и границ отделки — колонкой отметок слева. У знака — короткая марка; назначение, группа щита, высота и привязка каждой точки и вывода — в «Ведомости точек и выводов» под видами (каждая точка — строка).
3. У знака электроточки: марка (Р — розетка, S — выключатель, Св — светильник, ЭВ — вывод кабеля), ×N — число постов в рамке, гр. — группа щита, Н — высота оси от чистого пола, мм; группы по клавишам выключателя — на листе выключателей.
4. Схема мебели, приборов и декора не является технической документацией для производства мебели; габариты — по паспортам изделий.
5. Облицовка — по сетке швов, раскладка от оси стены (треугольник у пола); подрезки — по листу раскладки плитки.
6. Гидроизоляция в 2 слоя, заход на стены 200 мм — до облицовки, с актом скрытых работ и тестом проливом (узел — на листе узлов).
7. Картины и зеркала крепить к основанию по паспорту изделия (закладные и анкеры — в перечне скрытых работ); крест — ось центра предмета.
8. Двери скрытого монтажа — полотно в плоскости стены, отделка стены по полотну, плинтус прерывается у короба (узел — на листе узлов).

Допущения и предложения на листе

Основа листа: размеры сняты с растрового плана заказчика без размеров: масштаб восстановлен по площадям помещений (≈ 11,8 мм на пиксель), контрольный обмер не выполнен (К-1); высота потолка 2700 мм принята: на плане заказчика её нет (К-2); толщины стен 300 / 120 мм приняты по плану заказчика, не замерены (К-1); разрешённая мощность 15 кВт принята по типовым ТУ для квартиры, ТУ заказчиком не переданы (К-4); подрайон климата не задан — принят не северный (жилые от 2,5 м) (К-9).

Знак «**» — предложение проектировщика, заказчиком не утверждено (согласовать с заказчиком): ИЗ-4: ДК12.

См. лист открытых вопросов (лист 6, записи К-1, К-2, К-4; лист 7, запись К-9; лист 8, запись ИЗ-4).

1000 мм · печать 1:1

Изм.	Кол.уч	Лист	№ док.	Подп.	Дата
Разраб.		Кырлан А.С.			14.11.26
Пров.					
ГИП					
Н. контр.					
Утв.					

ГД-2026-007-АИ

Квартира 65 м²

Общая площадь 65,24* м² · * размеры со скана, не замерены (реестр — л. 6–8, К-1)

Дизайн-проект интерьера

Стадия	Лист	Листов
РП	94	117

Развёртки стен А, Б. Санузел (пом. 6)

М 1:20

Кырлан Александр Сергеевич


выпуск 14.11.2026 № 9cc0b98f36 · стр. 103 из 139

Развёртки стен В, Г. Санузел (пом. 6)

Санузел (пом. 6) · вид изнутри помещения · размеры в мм, отметки в м


ПРЕДВАРИТЕЛЬНО · не для производства работ · открыто пунктов: 14 (реестр — л. 6–8)

Стена В (М 1:20)

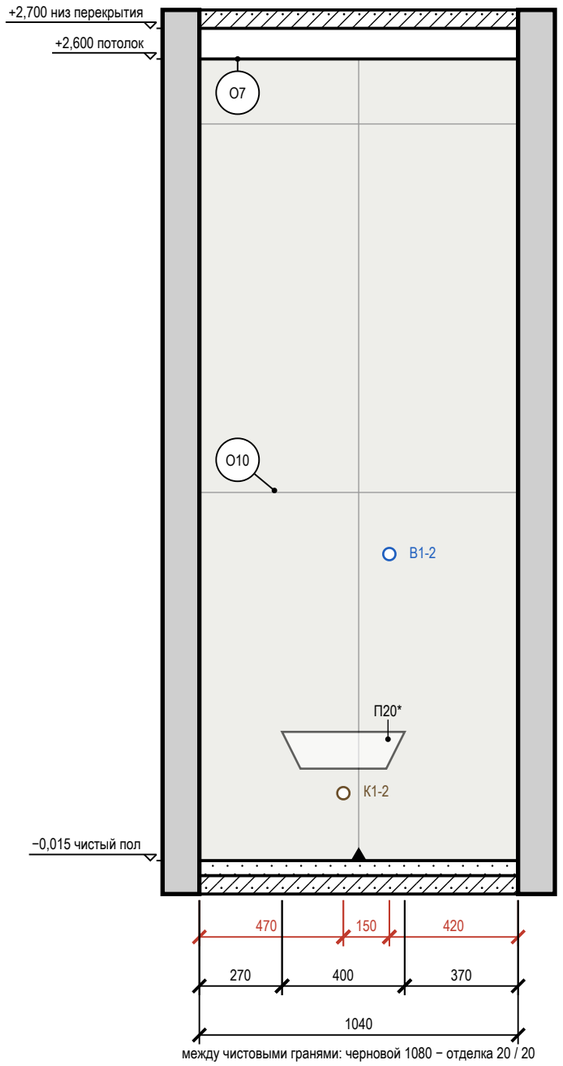

между чистовыми гранями: черновой 1080 − отделка 20 / 20

Стена Г (М 1:20)

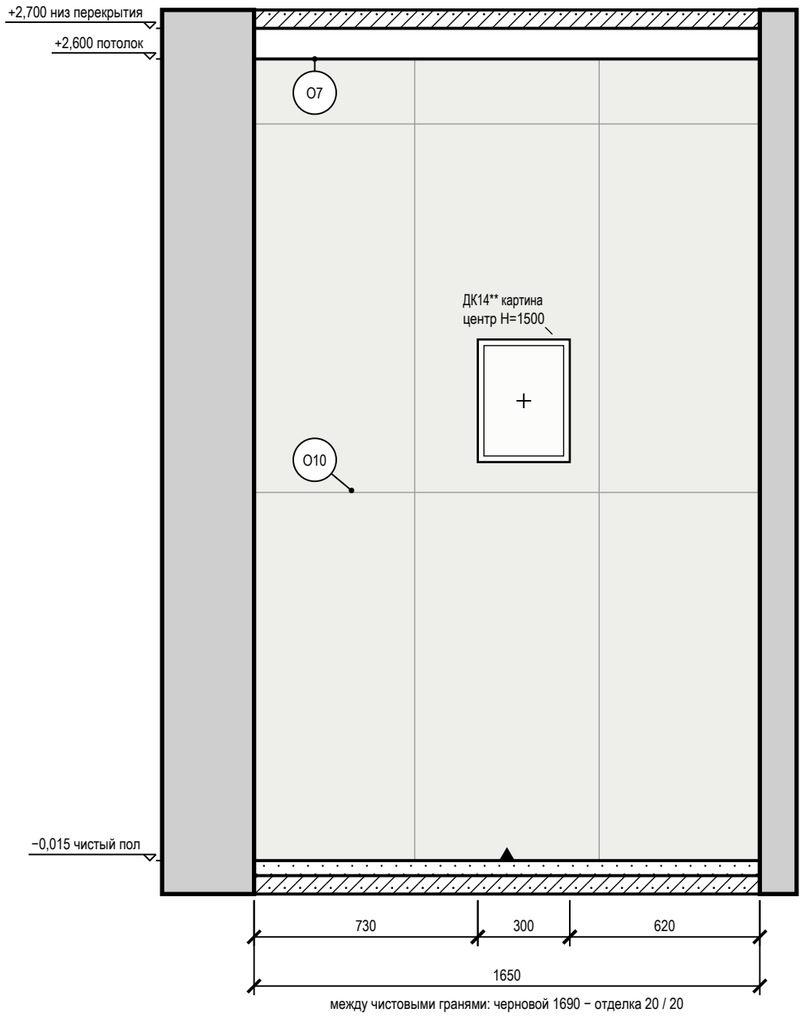

между чистовыми гранями: черновой 1690 − отделка 20 / 20

Ведомость точек и выводов

Стена	Марка	Что это	Гр.	Н, мм	От угла, мм	Примечание
В	К1-2	канализация — унитаз подвесной		220	470	Ø110
В	В1-2	холодная вода — унитаз подвесной		1000	620	в раме инсталляции


Условные обозначения

- вывод В1 (код — в ведомости привязок)
- вывод К1 (код — в ведомости привязок)
- привязки точек и выводов от угла и от пола, мм
- мебель и приборы — фасад по расстановке (условно)
- картина (декор): марка Д, крест — центр, Н — высота центра, мм
- стены и перекрытия в сечении
- плитка: сетка швов по формату, ▲ — ось старта
- О1 — марка отделки по реестру отделки альбома
- А — марка развёртки: буква стены, стрелка взгляд

Ведомость отделки (на листе)

Марка	Поверхность	Материал, изделие	Цвет, код	Кол.
О7	потолок	окраска, Tikkurila, глубокоматовая	NCS S 0300-N	1,8 м²
О10	стены	облицовка плиткой, Italon Charme Extra, 600×1200 мм, 610010001195	Italon 610010001195 «Charme Extra»	7 м²

Схема развёрток (М 1:50)

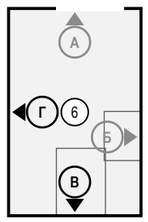

Ведомость изделий и проёмов (на листе)

Стена	Марка	Изделие, проём	На виде Ш×В, мм	Низ, мм
В	П20*	унитаз подвесной	400×120	300
Г	ДК14**	картина	300×400	1300

Примечания

1. Развёртки — вид на стену изнутри помещения, по часовой стрелке; расположение — на схеме листа и на листе 80; размеры — в мм по чистовым поверхностям; отметки — в м от ±0,000; высоты Н — от чистого пола помещения до оси изделия, у декора — до центра.
2. Красная цепочка — привязки электроточек и выводов по осям от угла чистовых стен; высота Н — у знака, от чистого пола до оси; высоты мебели, проёмов и границ отделки — колонкой отметок слева. У знака — короткая марка; назначение, группа щита, высота и привязка каждой точки и вывода — в «Ведомости точек и выводов» под видами (каждая точка — строка).
3. У знака электроточки: марка (Р — розетка, S — выключатель, Св — светильник, ЭВ — вывод кабеля), ×N — число постов в рамке, гр. — группа щита, Н — высота оси от чистого пола, мм; группы по клавишам выключателя — на листе выключателей.
4. Схема мебели, приборов и декора не является технической документацией для производства мебели; габариты — по паспортам изделий (* — высота не задана в проекте, показана по типовому изделию).
5. Облицовка — по сетке швов, раскладка от оси стены (треугольник у пола); подрезки — по листу раскладки плитки.
6. Гидроизоляция в 2 слоя, заход на стены 200 мм — до облицовки, с актом скрытых работ и тестом проливом (узел — на листе узлов).
7. Картины и зеркала крепить к основанию по паспорту изделия (закладные и анкеры — в перечне скрытых работ); крест — ось центра предмета.

Допущения и предложения на листе

Основа листа: размеры сняты с растрового плана заказчика без размеров: масштаб восстановлен по площадям помещений (≈ 11,8 мм на пиксель), контрольный обмер не выполнен (К-1); высота потолка 2700 мм принята: на плане заказчика её нет (К-2); толщины стен 300 / 120 мм приняты по плану заказчика, не замерены (К-1); разрешённая мощность 15 кВт принята по типовым ТУ для квартиры, ТУ заказчиком не переданы (К-4); подрайон климата не задан — принят не северный (жилые от 2,5 м) (К-9).
Знак «**» — предложение проектировщика, заказчиком не утверждено (согласовать с заказчиком): ИЗ-5: ДК14.
См. лист открытых вопросов (лист 6, записи К-1, К-2, К-4; лист 7, запись К-9; лист 8, запись ИЗ-5).

1000 мм · печать 1:1

Изм.	Кол.уч	Лист	№ док.	Подп.	Дата
Разраб.		Кырлан А.С.			14.11.26
Пров.					
ГИП					
Н. контр.					
Утв.					

ГД-2026-007-АИ

Квартира 65 м²

Общая площадь 65,24* м² · * размеры со скана, не замерены (реестр — л. 6–8, К-1)

Дизайн-проект интерьера

Стадия	Лист	Листов
РП	95	117

Развёртки стен В, Г. Санузел (пом. 6)

М 1:20

Кырлан Александр Сергеевич


выпуск 14.11.2026 № 9cc0b98f36 · стр. 104 из 139

Развёртки стен А, Б. Ванная (пом. 7)

Ванная (пом. 7) · вид изнутри помещения · размеры в мм, отметки в м


ПРЕДВАРИТЕЛЬНО · не для производства работ · открыто пунктов: 14 (реестр — л. 6–8)

Стена А (М 1:25)

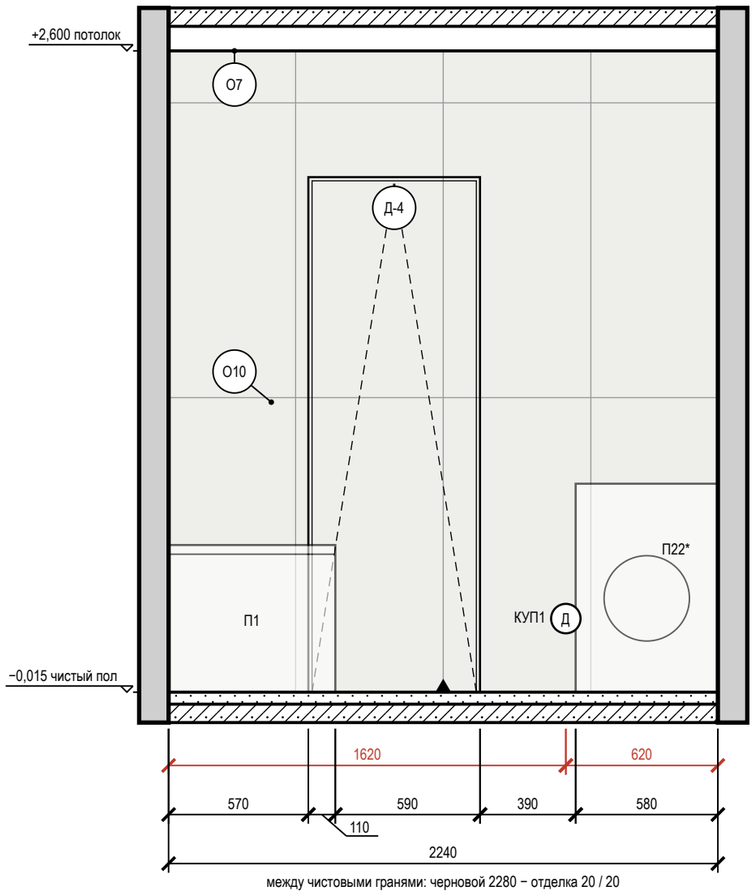

между чистовыми гранями: черновой 2280 − отделка 20 / 20

Стена Б (М 1:25)

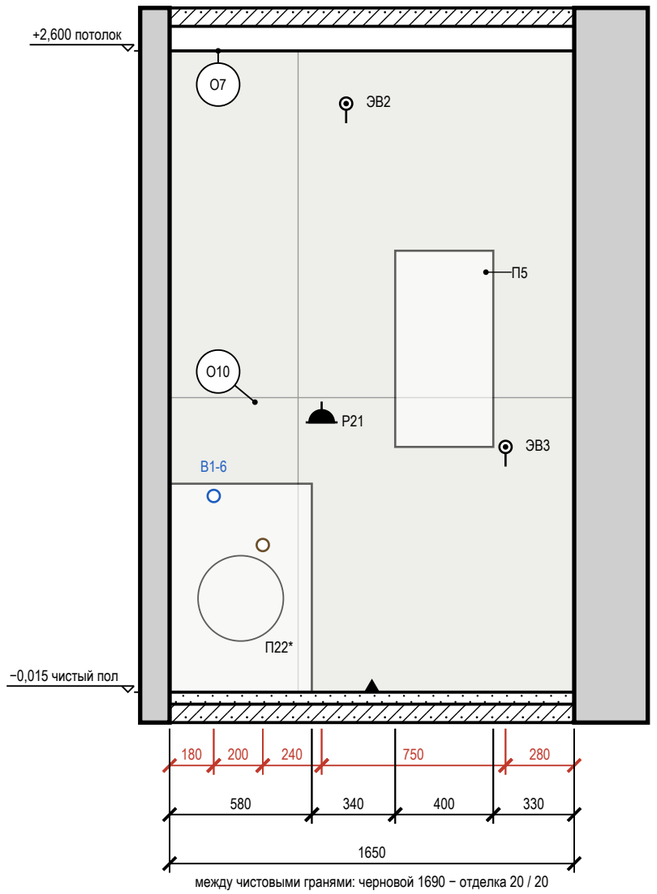

между чистовыми гранями: черновой 1690 − отделка 20 / 20

Ведомость точек и выводов

Стена	Марка	Что это	Гр.	Н, мм	От угла, мм	Примечание
А	КУП1	КУП (уравнивание потенциалов)		300	1620	
Б	В1-6	холодная вода — стиральная машина		800	180	кран машины
Б	К1-6	канализация — стиральная машина		600	380	Ø50
Б	Р21	розетка: стиральная машина	5	1100	620	IP44
Б	ЭВ2	вывод кабеля: вентилятор (клавиша L4, таймер выбега)	1	2400	720	
Б	ЭВ3	вывод кабеля: полотенцесушитель	5	1000	1370	


Условные обозначения

- розетка влагозащищённая IP44
- вывод кабеля для подключения прибора (без розетки), марка ЭВ
- вывод В1 (код — в ведомости привязок)
- вывод К1 (код — в ведомости привязок)
- привязки точек и выводов от угла и от пола, мм
- мебель и приборы — фасад по расстановке (условно)
- дверь скрытого монтажа: полотно в плоскости стены (узел — на листе узлов)
- стены и перекрытия в сечении
- плитка: сетка швов по формату, ▲ — ось старта
- О1 — марка отделки по реестру отделки альбома
- А — марка развёртки: буква стены, стрелка взгляд

Ведомость отделки (на листе)

Марка	Поверхность	Материал, изделие	Цвет, код	Кол.
О7	потолок	окраска, Tikkurila, глубокоматовая	NCS S 0300-N	3,9 м²
О10	стены	облицовка плиткой, Italon Charme Extra, 600×1200 мм, 610010001195	Italon 610010001195 «Charme Extra»	8,7 м²

Схема развёрток (М 1:50)

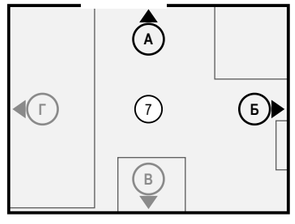

Примечания

1. Развёртки — вид на стену изнутри помещения, по часовой стрелке; расположение — на схеме листа и на листе 80; размеры — в мм по чистовым поверхностям; отметки — в м от ±0,000; высоты Н — от чистого пола помещения до оси изделия, у декора — до центра.
2. Красная цепочка — привязки электроточек и выводов по осям от угла чистовых стен; высота Н — у знака, от чистого пола до оси; высоты мебели, проёмов и границ отделки — колонкой отметок слева. У знака — короткая марка; назначение, группа щита, высота и привязка каждой точки и вывода — в «Ведомости точек и выводов» под видами (каждая точка — строка).
3. У знака электроточки: марка (Р — розетка, S — выключатель, Св — светильник, ЭВ — вывод кабеля), ×N — число постов в рамке, гр. — группа щита, Н — высота оси от чистого пола, мм; группы по клавишам выключателя — на листе выключателей.
4. Схема мебели, приборов и декора не является технической документацией для производства мебели; габариты — по паспортам изделий (* — высота не задана в проекте, показана по типовому изделию).
5. Облицовка — по сетке швов, раскладка от оси стены (треугольник у пола); подрезки — по листу раскладки плитки.
6. Гидроизоляция в 2 слоя, заход на стены 200 мм; над ванной — до 2000 и 300 мм за борт — до облицовки, с актом скрытых работ и тестом проливом (узел — на листе узлов).
7. Двери скрытого монтажа — полотно в плоскости стены, отделка стены по полотну, плинтус прерывается у короба (узел — на листе узлов).
8. Часть марок не уместилась у знаков: коды, высоты и привязки этих позиций — в ведомости точек и выводов под видами.

Допущения и предложения на листе

Основа листа: размеры сняты с растрового плана заказчика без размеров: масштаб восстановлен по площадям помещений (≈ 11,8 мм на пиксель), контрольный обмер не выполнен (К-1); высота потолка 2700 мм принята: на плане заказчика её нет (К-2); толщины стен 300 / 120 мм приняты по плану заказчика, не замерены (К-1); разрешённая мощность 15 кВт принята по типовым ТУ для квартиры, ТУ заказчиком не переданы (К-4); подрайон климата не задан — принят не северный (жилые от 2,5 м) (К-9).
См. лист открытых вопросов (лист 6, записи К-1, К-2, К-4; лист 7, запись К-9).

1000 мм · печать 1:1

Изм.	Кол.уч	Лист	№ док.	Подп.	Дата
Разраб.		Кырлан А.С.			14.11.26
Пров.					
ГИП					
Н. контр.					
Утв.					

ГД-2026-007-АИ

Квартира 65 м²

Общая площадь 65,24* м² · * размеры со скана, не замерены (реестр — л. 6–8, К-1)

Дизайн-проект интерьера	Стадия	Лист	Листов
	РП	96	117
Развёртки стен А, Б. Ванная (пом. 7) М 1:25	**Кырлан Александр Сергеевич**		


выпуск 14.11.2026 № 9cc0b98f36 · стр. 105 из 139

Развёртки стен В, Г. Ванная (пом. 7)

Ванная (пом. 7) · вид изнутри помещения · размеры в мм, отметки в м


ПРЕДВАРИТЕЛЬНО · не для производства работ · открыто пунктов: 14 (реестр — л. 6–8)

Стена В (М 1:25)

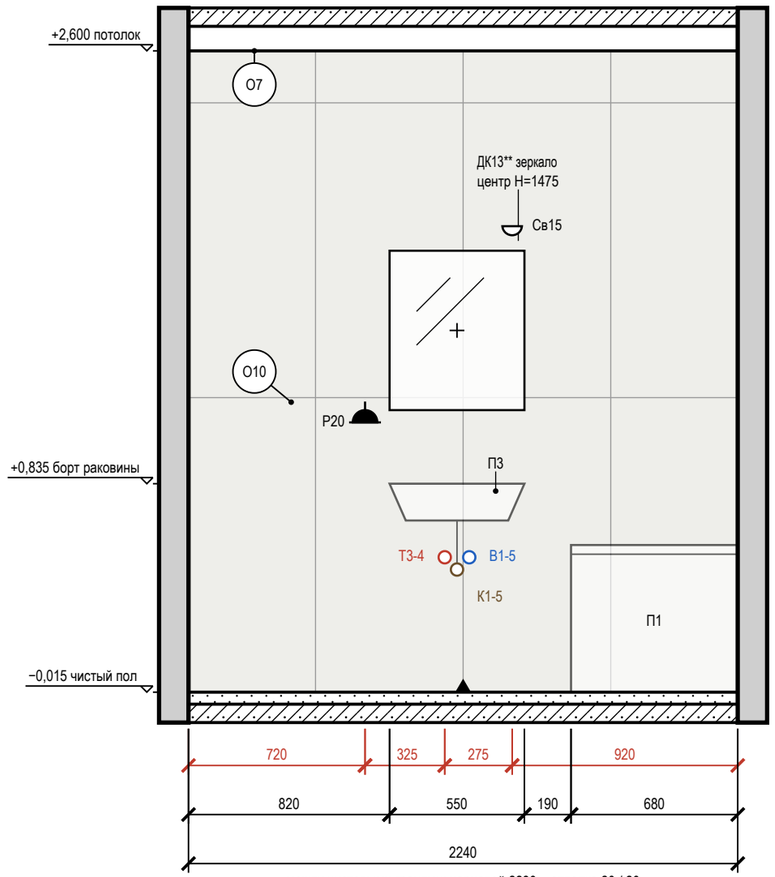

между чистовыми гранями: черновой 2280 − отделка 20 / 20

Стена Г (М 1:25)

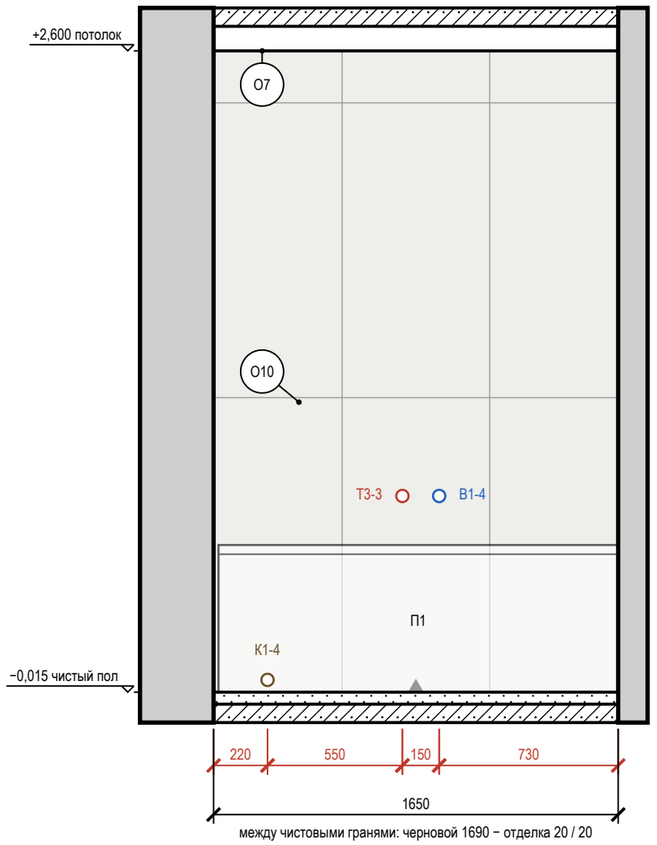

между чистовыми гранями: черновой 1690 − отделка 20 / 20

Ведомость точек и выводов

Стена	Марка	Что это	Гр.	Н, мм	От угла, мм	Примечание
В	Р20	розетка: фен	5	1100	720	IP44
В	Т3-4	горячая вода — умывальник		550	1045	межос. 100
В	К1-5	канализация — умывальник		500	1095	Ø50
В	В1-5	холодная вода — умывальник		550	1145	межос. 100
В	Св15	светильник настенный	1	1900	1320	
Г	К1-4	канализация — ванна		50	220	Ø50
Г	Т3-3	горячая вода — ванна		800	770	межос. 150
Г	В1-4	холодная вода — ванна		800	920	межос. 150


Условные обозначения

- розетка влагозащищённая IP44
- светильник настенный (бра), Н — высота оси
- вывод В1 (код — в ведомости привязок)
- вывод Т3 (код — в ведомости привязок)
- вывод К1 (код — в ведомости привязок)
- привязки точек и выводов от угла и от пола, мм
- мебель и приборы — фасад по расстановке (условно)
- зеркало: марка Д, крест — центр, Н — высота центра, мм
- стены и перекрытия в сечении
- плитка: сетка швов по формату, ▲ — ось старта
- О1 — марка отделки по реестру отделки альбома
- А — марка развёртки: буква стены, стрелка взгляд

Ведомость отделки (на листе)

Марка	Поверхность	Материал, изделие	Цвет, код	Кол.
О7	потолок	окраска, Tikkurila, глубокоматовая	NCS S 0300-N	3,9 м²
О10	стены	облицовка плиткой, Italon Charme Extra, 600×1200 мм, 610010001195	Italon 610010001195 «Charme Extra»	10,2 м²

Схема развёрток (М 1:100)

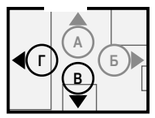

Примечания

1. Развёртки — вид на стену изнутри помещения, по часовой стрелке; расположение — на схеме листа и на листе 80; размеры — в мм по чистовым поверхностям; отметки — в м от ±0,000; высоты Н — от чистого пола помещения до оси изделия, у декора — до центра.
2. Красная цепочка — привязки электроточек и выводов по осям от угла чистовых стен; высота Н — у знака, от чистого пола до оси; высоты мебели, проёмов и границ отделки — колонкой отметок слева. У знака — короткая марка; назначение, группа щита, высота и привязка каждой точки и вывода — в «Ведомости точек и выводов» под видами (каждая точка — строка).
3. У знака электроточки: марка (Р — розетка, S — выключатель, Св — светильник, ЭВ — вывод кабеля), ×N — число постов в рамке, гр. — группа щита, Н — высота оси от чистого пола, мм; группы по клавишам выключателя — на листе выключателей.
4. Схема мебели, приборов и декора не является технической документацией для производства мебели; габариты — по паспортам изделий.
5. Облицовка — по сетке швов, раскладка от оси стены (треугольник у пола); подрезки — по листу раскладки плитки.
6. Гидроизоляция в 2 слоя, заход на стены 200 мм; над ванной — до 2000 и 300 мм за борт — до облицовки, с актом скрытых работ и тестом проливом (узел — на листе узлов).
7. Картины и зеркала крепить к основанию по паспорту изделия (закладные и анкеры — в перечне скрытых работ); крест — ось центра предмета.

Допущения и предложения на листе

Основа листа: размеры сняты с растрового плана заказчика без размеров: масштаб восстановлен по площадям помещений (≈ 11,8 мм на пиксель), контрольный обмер не выполнен (К-1); высота потолка 2700 мм принята: на плане заказчика её нет (К-2); толщины стен 300 / 120 мм приняты по плану заказчика, не замерены (К-1); разрешённая мощность 15 кВт принята по типовым ТУ для квартиры, ТУ заказчиком не переданы (К-4); подрайон климата не задан — принят не северный (жилые от 2,5 м) (К-9).

Знак «**» — предложение проектировщика, заказчиком не утверждено (согласовать с заказчиком): ИЗ-4: ДК13.

См. лист открытых вопросов (лист 6, записи К-1, К-2, К-4; лист 7, запись К-9; лист 8, запись ИЗ-4).

1000 мм · печать 1:1

Изм.	Кол.уч	Лист	№ док.	Подп.	Дата
Разраб.		Кырлан А.С.			14.11.26
Пров.					
ГИП					
Н. контр.					
Утв.					

ГД-2026-007-АИ

Квартира 65 м²

Общая площадь 65,24* м² · * размеры со скана, не замерены (реестр — л. 6–8, К-1)

Дизайн-проект интерьера

Стадия	Лист	Листов
РП	97	117

Развёртки стен В, Г. Ванная (пом. 7)

М 1:25

Кырлан Александр Сергеевич


выпуск 14.11.2026 № 9cc0b98f36 · стр. 106 из 139

Развёртки стен. Кладовая (пом. 8)

Кладовая (пом. 8) · вид изнутри помещения · размеры в мм, отметки в м


ПРЕДВАРИТЕЛЬНО · не для производства работ · открыто пунктов: 14 (реестр — л. 6–8)

Стена А (М 1:25)

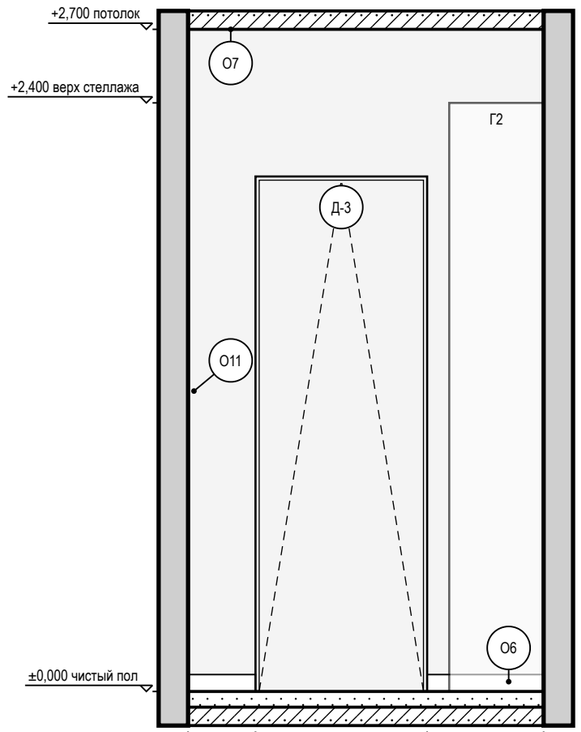


между чистовыми гранями: черновой 1480 − отделка 15 / 15

Стена Б (М 1:25)

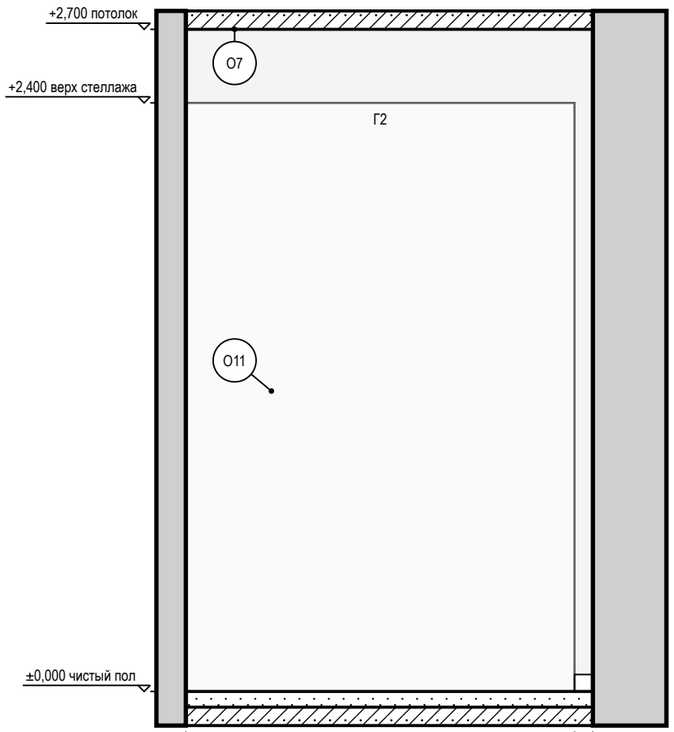

между чистовыми гранями: черновой 1690 − отделка 15 / 15

Стена В (М 1:25)

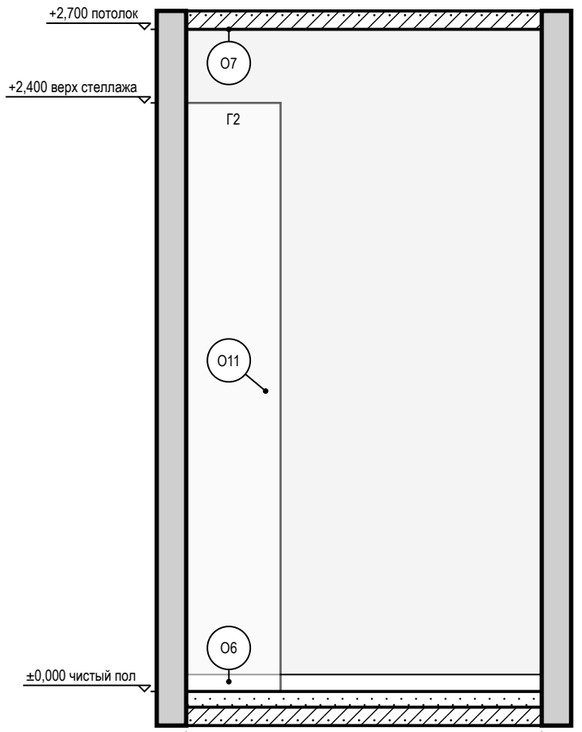

между чистовыми гранями: черновой 1480 − отделка 15 / 15


Условные обозначения

- мебель и приборы — фасад по расстановке (условно)
- дверь скрытого монтажа: полотно в плоскости стены (узел — на листе узлов)
- стены и перекрытия в сечении
- О1 — марка отделки по реестру отделки альбома
- А — марка развёртки: буква стены, стрелка — взгляд

Ведомость отделки (на листе)

Марка	Поверхность	Материал, изделие	Цвет, код	Кол.
О6	плинтус	плинтус МДФ, Orac Decor Contour (Luxxus), h 69 мм, SX165, шелковисто-матовая	NCS S 0300-N	2,3 м
О7	потолок	окраска, Tikkurila, глубокоматовая	NCS S 0300-N	2,5 м²
О11	стены	окраска, Tikkurila, матовая, подготовка Q3	NCS S 0502-Y	10,8 м²

Схема развёрток (М 1:50)

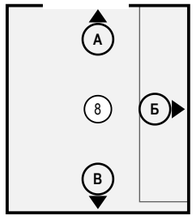

Ведомость изделий и проёмов (на листе)

Стена	Марка	Изделие, проём	На виде Ш×В, мм	Низ, мм
А	Д-3	дверь скрытого монтажа	700×2100	0
А	Г2	стеллаж кладовой	385×2400	0
Б	Г2	стеллаж кладовой	1585×2400	0
В	Г2	стеллаж кладовой	385×2400	0

Примечания

1. Развёртки — вид на стену изнутри помещения, по часовой стрелке; расположение — на схеме листа и на листе 80; размеры — в мм по чистовым поверхностям; отметки — в м от ±0,000; высоты Н — от чистого пола помещения до оси изделия, у декора — до центра.
2. Схема мебели, приборов и декора не является технической документацией для производства мебели; габариты — по паспортам изделий.
3. Двери скрытого монтажа — полотно в плоскости стены, отделка стены по полотну, плинтус прерывается у короба (узел — на листе узлов).

Допущения и предложения на листе

Основа листа: размеры сняты с растрового плана заказчика без размеров: масштаб восстановлен по площадям помещений (≈ 11,8 мм на пиксель), контрольный обмер не выполнен (К-1); высота потолка 2700 мм принята: на плане заказчика её нет (К-2); толщины стен 300 / 120 мм приняты по плану заказчика, не замерены (К-1); разрешённая мощность 15 кВт принята по типовым ТУ для квартиры, ТУ заказчиком не переданы (К-4); подрайон климата не задан — принят не северный (жилые от 2,5 м) (К-9).
См. лист открытых вопросов (лист 6, записи К-1, К-2, К-4; лист 7, запись К-9).

1000 мм · печать 1:1

Изм.	Кол.уч	Лист	№ док.	Подп.	Дата
Разраб.		Кырлан А.С.			14.11.26
Пров.					
ГИП					
Н. контр.					
Утв.					

ГД-2026-007-АИ

Квартира 65 м²

Общая площадь 65,24* м² · * размеры со скана, не замерены (реестр — л. 6–8, К-1)

Дизайн-проект интерьера

Стадия	Лист	Листов
РП	98	117

Развёртки стен. Кладовая (пом. 8)

М 1:25

Кырлан Александр Сергеевич


выпуск 14.11.2026 № 9cc0b98f36 · стр. 107 из 139

Развёртка стены А. Детская (пом. 9)

Детская (пом. 9) · вид изнутри помещения · размеры в мм, отметки в м

ПРЕДВАРИТЕЛЬНО · не для производства работ · открыто пунктов: 14 (реестр — л. 6–8)

Стена А (М 1:25)

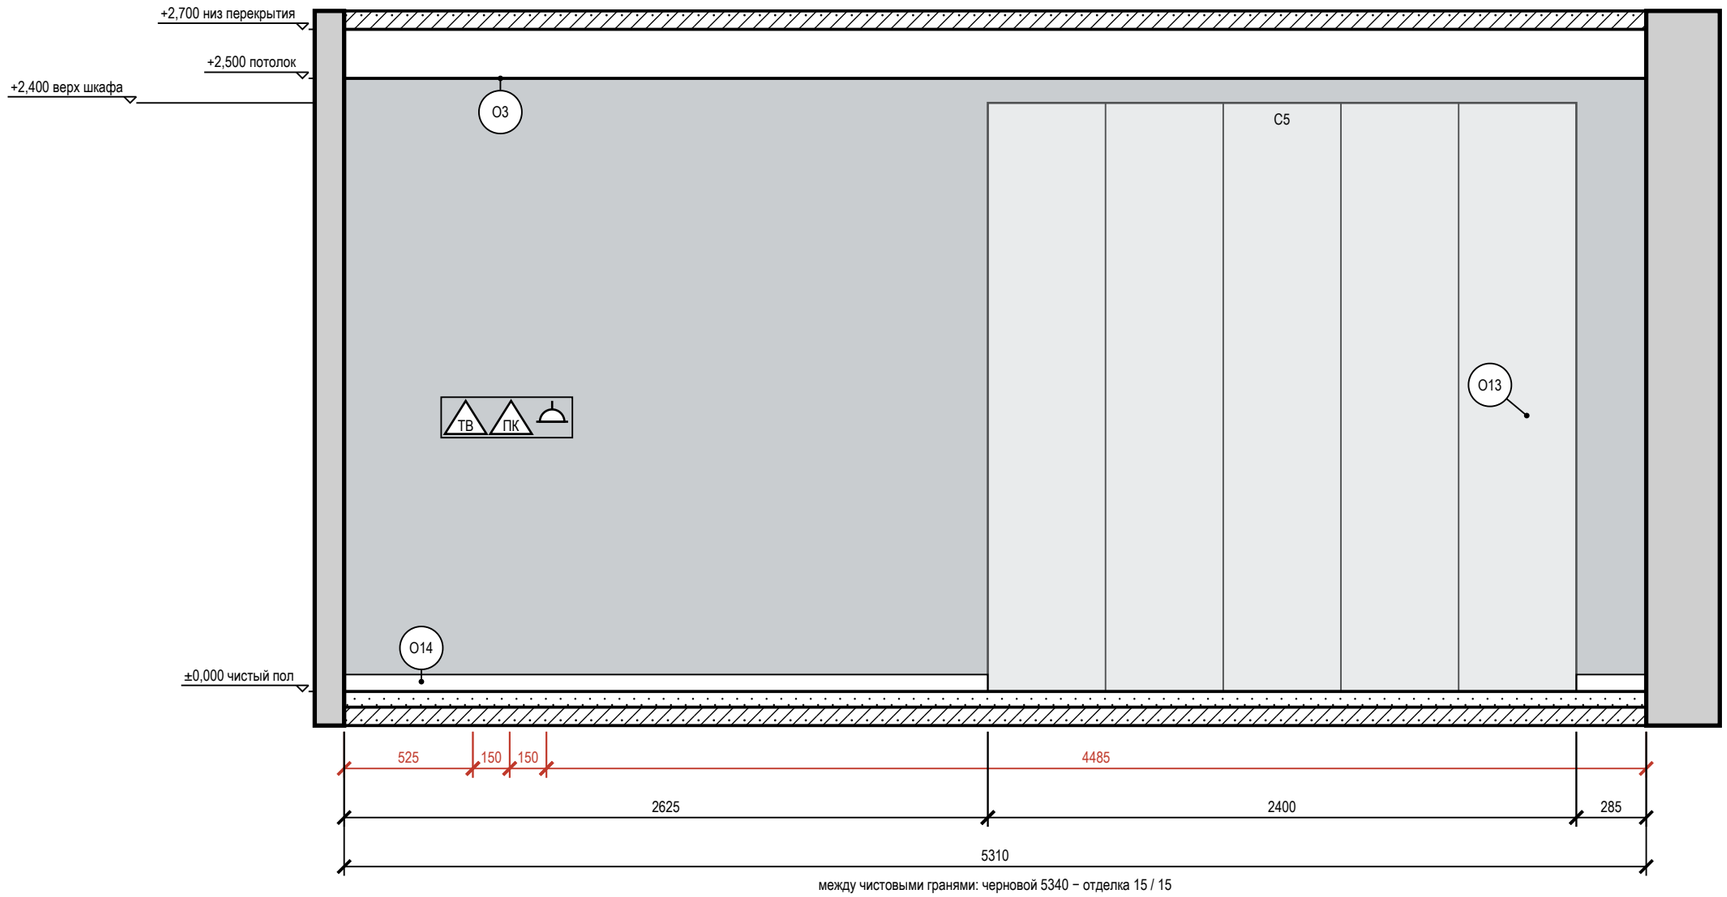


между чистовыми гранями: черновой 5340 − отделка 15 / 15

Условные обозначения

- розетка с заземляющим контактом; у знака — марка, ×N постов в рамке, гр. — группа щита, Н — высота оси, мм
- ПК — розетка компьютерная RJ45
- ТВ — розетка телевизионная
- привязки точек и выводов от угла и от пола, мм
- мебель и приборы — фасад по расстановке (условно)
- стены и перекрытия в сечении
- окраска: тон — цвет по коду производителя (условно)
- О1 — марка отделки по реестру отделки альбома
- А — марка развёртки: буква стены, стрелка — взгляд

Схема развёрток (М 1:100)

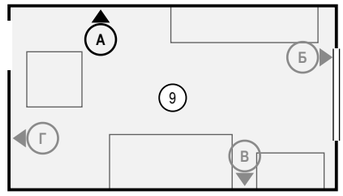

Ведомость точек и выводов

Марка	Что это	Гр.	Н, мм	От угла, мм	Примечание
ТВ2	розетка ТВ: ТВ на стене А, кронштейн (мебели под ТВ нет)		1100	525	

Марка	Что это	Гр.	Н, мм	От угла, мм	Примечание
LAN4	розетка RJ45: Smart TV		1100	675	

Марка	Что это	Гр.	Н, мм	От угла, мм	Примечание
Р12**	розетка: ТВ (в одной зоне с ТВ2, LAN4 на стене А)	5	1100	825	

Примечания

1. Развёртки — вид на стену изнутри помещения, по часовой стрелке; расположение — на схеме листа и на листе 80; размеры — в мм по чистовым поверхностям; отметки — в м от ±0,000; высоты Н — от чистого пола помещения до оси изделия, у декора — до центра.
2. Красная цепочка — привязки электроточек и выводов по осям от угла чистовых стен; высота Н — у знака, от чистого пола до оси; высоты мебели, проёмов и границ отделки — колонкой отметок слева. У знака — короткая марка; назначение, группа щита, высота и привязка каждой точки и вывода — в «Ведомости точек и выводов» под видами (каждая точка — строка).
3. Отделка стен — по ведомости отделки помещений, лист 57.
4. У знака электроточки: марка (Р — розетка, S — выключатель, Св — светильник, ЭВ — вывод кабеля), ×N — число постов в рамке, гр. — группа щита, Н — высота оси от чистого пола, мм; группы по клавишам выключателя — на листе выключателей.
5. Схема мебели, приборов и декора не является технической документацией для производства мебели; габариты — по паспортам изделий.
6. Потолок — у каждой стены свой, по плану потолков (ПТ3); ступени — зоной, кромка короба перед нишей — тонкой линией; в поле потолка: ПТ1 +2,600.
7. Часть марок не уместилась у знаков: коды, высоты и привязки этих позиций — в ведомости точек и выводов под видами.

Допущения и предложения на листе

Основа листа: размеры сняты с растрового плана заказчика без размеров: масштаб восстановлен по площадям помещений (≈ 11,8 мм на пиксель), контрольный обмер не выполнен (К-1); высота потолка 2700 мм принята: на плане заказчика её нет (К-2); толщины стен 300 / 120 мм приняты по плану заказчика, не замерены (К-1); разрешённая мощность 15 кВт принята по типовым ТУ для квартиры, ТУ заказчиком не переданы (К-4); подрайон климата не задан — принят не северный (жилые от 2,5 м) (К-9).

Знак «**» — предложение проектировщика, заказчиком не утверждено (согласовать с заказчиком): Р12 — Было: стена В смещение 1985, назначение «ТВ над комодом» — над кроватью С6, ТВ2 и LAN4 при этом на стене А, комода в помещении нет (назначение по шаблону).

См. лист открытых вопросов (лист 6, записи К-1, К-2, К-4; лист 7, запись К-9).

1000 мм · печать 1:1

Изм.	Кол.уч	Лист	№ док.	Подп.	Дата
Разраб.		Кырлан А.С.			14.11.26
Пров.					
ГИП					
Н. контр.					
Утв.					

ГД-2026-007-АИ

Квартира 65 м²

Общая площадь 65,24* м² · * размеры со скана, не замерены (реестр — л. 6–8, К-1)

Дизайн-проект интерьера

Стадия	Лист	Листов
РП	99	117

Развёртка стены А. Детская (пом. 9)

М 1:25

Кырлан Александр Сергеевич


выпуск 14.11.2026 № 9cc0b98f36 · стр. 108 из 139

Развёртка стены Б. Детская (пом. 9)

Детская (пом. 9) · вид изнутри помещения · размеры в мм, отметки в м

ПРЕДВАРИТЕЛЬНО · не для производства работ · открыто пунктов: 14 (реестр — л. 6–8)

Стена Б (М 1:20)

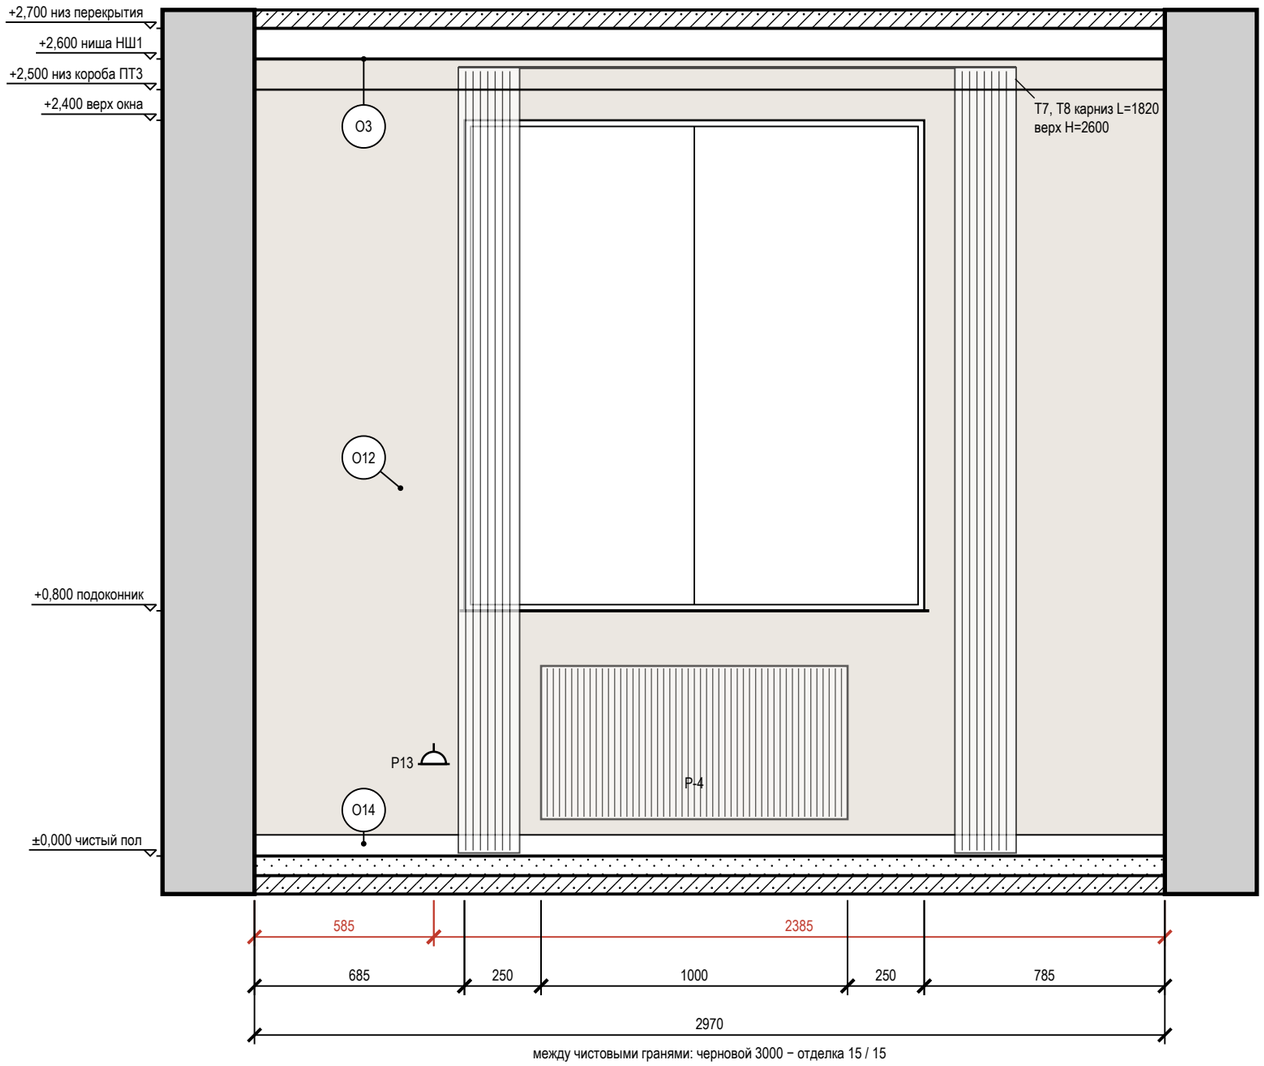

между чистовыми гранями: черновой 3000 − отделка 15 / 15

Ведомость точек и выводов

Марка	Что это	Гр.	H, мм	От угла, мм	Примечание
Р13	розетка: уборка	5	300	585	


Условные обозначения

- розетка с заземляющим контактом; у знака — марка, ×N постов в рамке, гр. — группа щита, H — высота оси, мм
- привязки точек и выводов от угла и от пола, мм
- мебель и приборы — фасад по расстановке (условно)
- карниз (шина) и шторы в собранном виде: марка T, длина L, верх H
- окно: проём, рама, подоконник
- радиатор отопления; марка — по плану отопления
- стены и перекрытия в сечении
- окраска: тон — цвет по коду производителя (условно)
- О1 — марка отделки по реестру отделки альбома
- А — марка развёртки: буква стены, стрелка — взгляд

Ведомость отделки (на листе)

Марка	Поверхность	Материал, изделие	Цвет, код	Кол.
О3	потолок	окраска, Tikkurila Anti-Reflex 2, глубокоматовая, подготовка Q3	Tikkurila V503 «Winter»	16 м²
О12	стены	окраска, Farrow & Ball Modern Emulsion, матовая, подготовка Q3	Farrow & Ball No. 241 «Skimming Stone»	5,3 м²
О14	плинтус	плинтус МДФ, Orac Decor Contour (Luxxus), h 69 мм, SX165	Farrow & Ball No. 241 «Skimming Stone»	3 м

Схема развёрток (М 1:100)

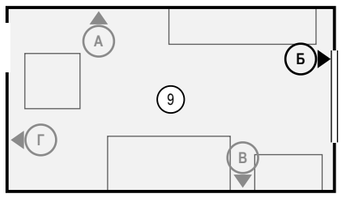

Ведомость изделий и проёмов (на листе)

Марка	Изделие, проём	На виде Ш×В, мм	Низ, мм
Р-4	радиатор отопления	1000×500	120

Примечания

1. Развёртки — вид на стену изнутри помещения, по часовой стрелке; расположение — на схеме листа и на листе 80; размеры — в мм по чистовым поверхностям; отметки — в м от ±0,000; высоты H — от чистого пола помещения до оси изделия, у декора — до центра.
2. Красная цепочка — привязки электроточек и выводов по осям от угла чистовых стен; высота H — у знака, от чистого пола до оси; высоты мебели, проёмов и границ отделки — колонкой отметок слева. У знака — короткая марка; назначение, группа щита, высота и привязка каждой точки и вывода — в «Ведомости точек и выводов» под видами (каждая точка — строка).
3. У знака электроточки: марка (Р — розетка, S — выключатель, Св — светильник, ЭВ — вывод кабеля), ×N — число постов в рамке, гр. — группа щита, H — высота оси от чистого пола, мм; группы по клавишам выключателя — на листе выключателей.
4. Схема мебели, приборов и декора не является технической документацией для производства мебели; габариты — по паспортам изделий.
5. Карнизы (шины) — по ведомости текстиля декоратора: длина L и верх H на развёртке — те же числа, что в ведомости; крепление — до окраски потолка.
6. Потолок — у каждой стены свой, по плану потолков (НШ1, ПТ3); ступени — зоной, кромка короба перед нишей — тонкой линией; в поле потолка: ПТ1 +2,600.

Допущения и предложения на листе

Основа листа: размеры сняты с растрового плана заказчика без размеров: масштаб восстановлен по площадям помещений (≈ 11,8 мм на пиксель), контрольный обмер не выполнен (К-1); высота потолка 2700 мм принята: на плане заказчика её нет (К-2); толщины стен 300 / 120 мм приняты по плану заказчика, не замерены (К-1); разрешённая мощность 15 кВт принята по типовым ТУ для квартиры, ТУ заказчиком не переданы (К-4); подрайон климата не задан — принят не северный (жилые от 2,5 м) (К-9).
См. лист открытых вопросов (лист 6, записи К-1, К-2, К-4; лист 7, запись К-9).

1000 мм · печать 1:1

Изм.	Кол.уч	Лист	№ док.	Подп.	Дата
Разраб.		Кырлан А.С.			14.11.26
Пров.					
ГИП					
Н. контр.					
Утв.					

ГД-2026-007-АИ

Квартира 65 м²

Общая площадь 65,24* м² · * размеры со скана, не замерены (реестр — л. 6–8, К-1)

Дизайн-проект интерьера

Стадия	Лист	Листов
РП	100	117

Развёртка стены Б. Детская (пом. 9)

М 1:20

Кырлан Александр Сергеевич


выпуск 14.11.2026 № 9cc0b98f36 · стр. 109 из 139

Развёртка стены В. Детская (пом. 9)

Детская (пом. 9) · вид изнутри помещения · размеры в мм, отметки в м

ПРЕДВАРИТЕЛЬНО · не для производства работ · открыто пунктов: 14 (реестр — л. 6–8)

Стена В (М 1:25)

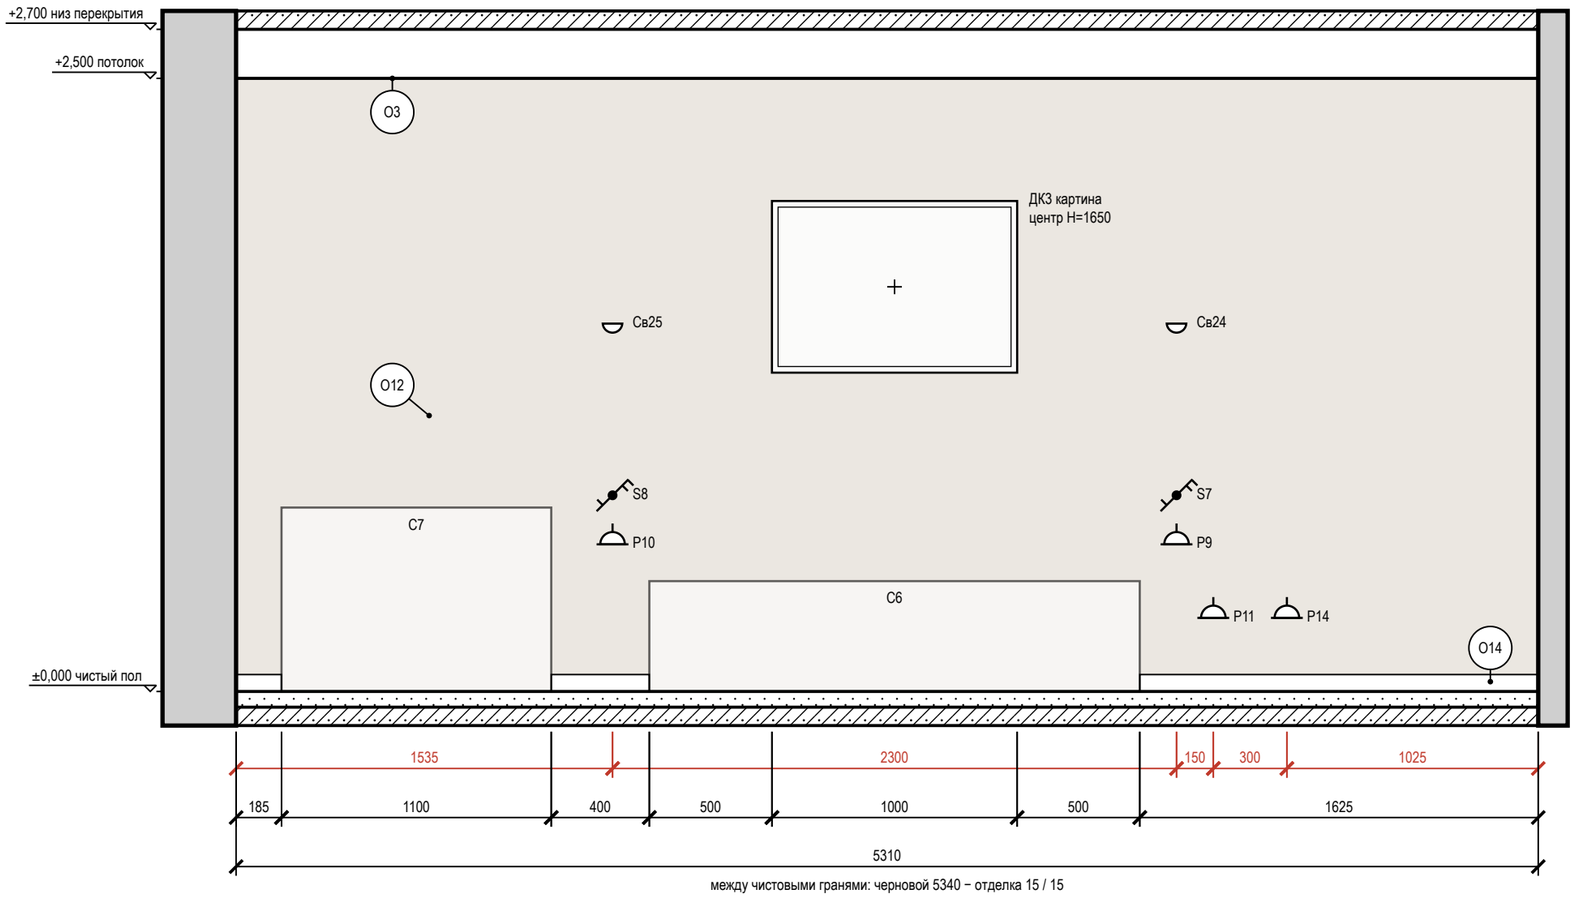

между чистовыми гранями: черновой 5340 − отделка 15 / 15


Ведомость точек и выводов

Марка	Что это	Гр.	Н, мм	От угла, мм	Примечание
P10	розетка: у кровати	5	600	1535	
S8	выключатель	1	800	1535	
Св25	светильник настенный	1	1500	1535	
P9	розетка: у кровати	5	600	3835	
S7	выключатель	1	800	3835	
Св24	светильник настенный	1	1500	3835	
P11	розетка: торшер у кровати С6 (изголовье)	5	300	3985	
P14	розетка: уборка у входа	5	300	4285	

Условные обозначения

- розетка с заземляющим контактом; у знака — марка, ×N постов в рамке, гр. — группа щита, Н — высота оси, мм
- выключатель одноклавишный
- выключатель двухклавишный (флажков — по числу клавиш)
- выключатель с проходной или перекрёстной клавишей (обратный флажок); тип клавиши — в подписи
- светильник настенный (бра), Н — высота оси
- привязки точек и выводов от угла и от пола, мм
- мебель и приборы — фасад по расстановке (условно)
- картина (декор): марка Д, крест — центр, Н — высота центра, мм
- стены и перекрытия в сечении
- окраска: тон — цвет по коду производителя (условно)
- О1 — марка отделки по реестру отделки альбома
- А — марка развёртки: буква стены, стрелка — взгляд

Схема развёрток (М 1:100)

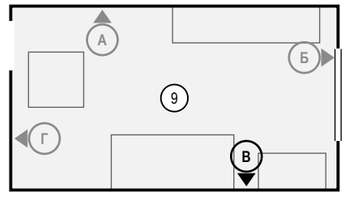

Ведомость изделий и проёмов (на листе)

Марка	Изделие, проём	На виде Ш×В, мм	Низ, мм
С7	стол письменный	1100×750	0
С6	кровать односпальная 900×2000	2000×450	0
ДК3	картина	1000×700	1300

Примечания

1. Развёртки — вид на стену изнутри помещения, по часовой стрелке; расположение — на схеме листа и на листе 80; размеры — в мм по чистовым поверхностям; отметки — в м от ±0,000; высоты Н — от чистого пола помещения до оси изделия, у декора — до центра.
2. Красная цепочка — привязки электроточек и выводов по осям от угла чистовых стен; высота Н — у знака, от чистого пола до оси; высоты мебели, проёмов и границ отделки — колонкой отметок слева. У знака — короткая марка; назначение, группа щита, высота и привязка каждой точки и вывода — в «Ведомости точек и выводов» под видами (каждая точка — строка).
3. Отделка стен — по ведомости отделки помещений, лист 57.
4. У знака электроточки: марка (Р — розетка, S — выключатель, Св — светильник, ЭВ — вывод кабеля), ×N — число постов в рамке, гр. — группа щита, Н — высота оси от чистого пола, мм; группы по клавишам выключателя — на листе выключателей.
5. Схема мебели, приборов и декора не является технической документацией для производства мебели; габариты — по паспортам изделий.
6. Картины и зеркала крепить к основанию по паспорту изделия (закладные и анкеры — в перечне скрытых работ); крест — ось центра предмета.
7. Потолок — у каждой стены свой, по плану потолков (ПТ3); ступени — зоной, кромка короба перед нишей — тонкой линией; в поле потолка: ПТ1 +2,600.

Допущения и предложения на листе

Основа листа: размеры сняты с растрового плана заказчика без размеров: масштаб восстановлен по площадям помещений (≈ 11,8 мм на пиксель), контрольный обмер не выполнен (К-1); высота потолка 2700 мм принята: на плане заказчика её нет (К-2); толщины стен 300 / 120 мм приняты по плану заказчика, не замерены (К-1); разрешённая мощность 15 кВт принята по типовым ТУ для квартиры, ТУ заказчиком не переданы (К-4); подрайон климата не задан — принят не северный (жилые от 2,5 м) (К-9).

См. лист открытых вопросов (лист 6, записи К-1, К-2, К-4; лист 7, запись К-9).

1000 мм · печать 1:1

						ГД-2026-007-АИ	
						Квартира 65 м²	
						Общая площадь 65,24* м² · * размеры со скана, не замерены (реестр — л. 6–8, К-1)	
Изм.	Кол.уч	Лист	№ док.	Подп.	Дата	Дизайн-проект интерьера	Стадия: РП; Лист: 101; Листов: 117
Разраб.		Кырлан А.С.			14.11.26	**Развёртка стены В. Детская (пом. 9)** М 1:25	**Кырлан Александр Сергеевич**
Пров.							
ГИП							
Н. контр.							
Утв.							


выпуск 14.11.2026 № 9cc0b98f36 · стр. 110 из 139

Развёртка стены Г. Детская (пом. 9)

Детская (пом. 9) · вид изнутри помещения · размеры в мм, отметки в м

ПРЕДВАРИТЕЛЬНО · не для производства работ · открыто пунктов: 14 (реестр — л. 6–8)

Стена Г (М 1:20)

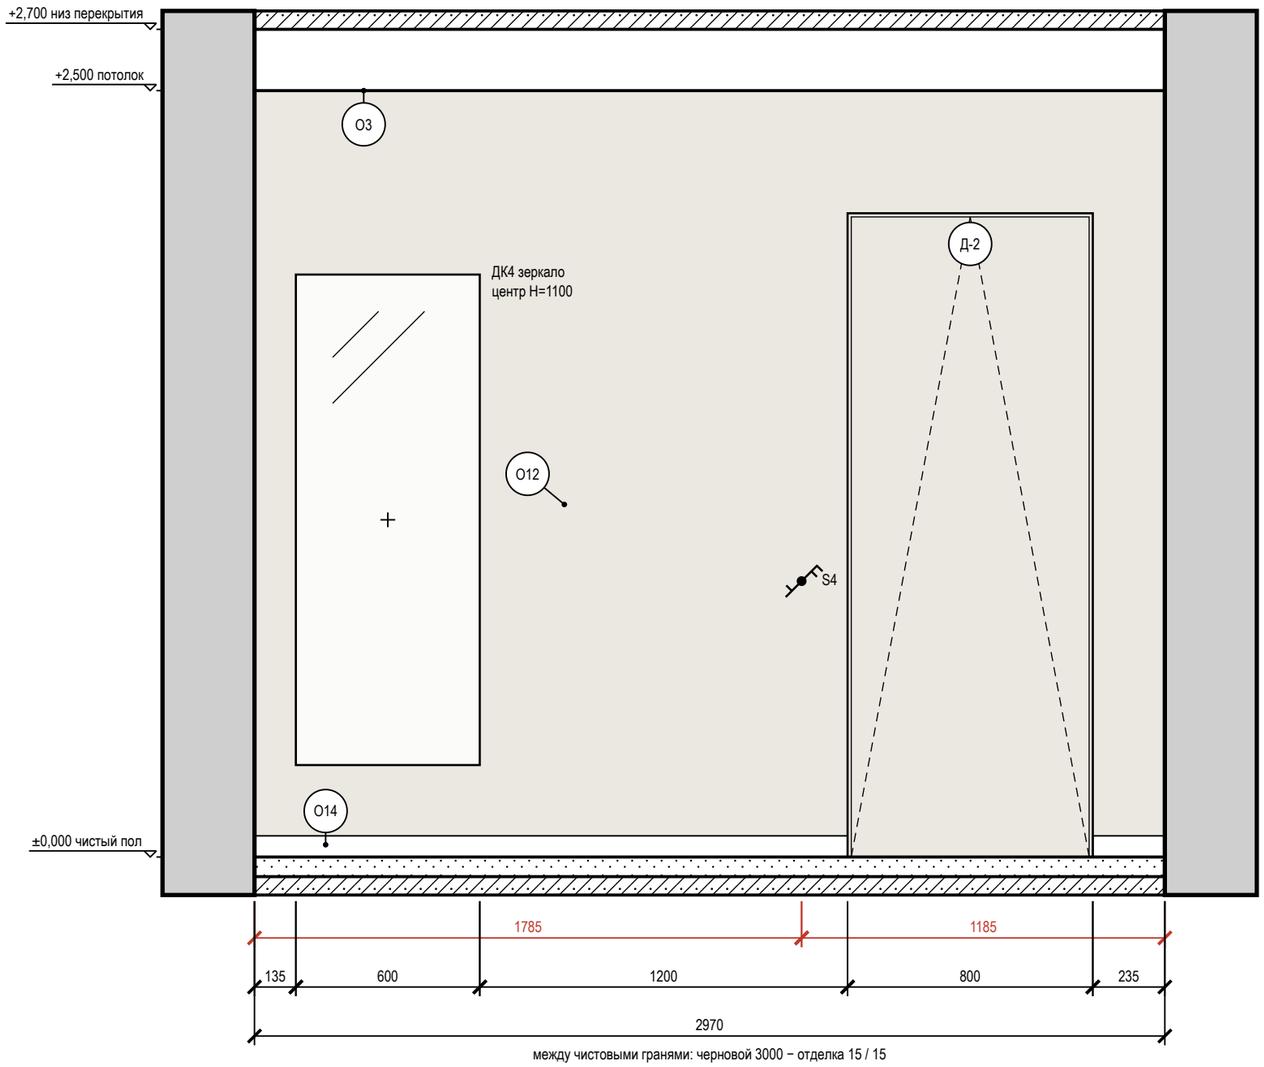

между чистовыми гранями: черновой 3000 − отделка 15 / 15

Ведомость точек и выводов

Марка	Что это	Гр.	Н, мм	От угла, мм	Примечание
S4	выключатель	1	900	1785	


Условные обозначения

- выключатель одноклавишный
- выключатель двухклавишный (флажков — по числу клавиш)
- выключатель с проходной или перекрёстной клавишей (обратный флажок); тип клавиши — в подписи
- привязки точек и выводов от угла и от пола, мм
- мебель и приборы — фасад по расстановке (условно)
- зеркало: марка Д, крест — центр, Н — высота центра, мм
- дверь скрытого монтажа: полотно в плоскости стены (узел — на листе узлов)
- стены и перекрытия в сечении
- окраска: тон — цвет по коду производителя (условно)
- О1 — марка отделки по реестру отделки альбома
- А — марка развёртки: буква стены, стрелка — взгляд

Ведомость отделки (на листе)

Марка	Поверхность	Материал, изделие	Цвет, код	Кол.
О3	потолок	окраска, Tikkurila Anti-Reflex 2, глубокоматовая, подготовка Q3	Tikkurila V503 «Winter»	16 м²
О12	стены	окраска, Farrow & Ball Modern Emulsion, матовая, подготовка Q3	Farrow & Ball No. 241 «Skimming Stone»	5,7 м²
О14	плинтус	плинтус МДФ, Orac Decor Contour (Luxxus), h 69 мм, SX165	Farrow & Ball No. 241 «Skimming Stone»	2,2 м

Схема развёрток (М 1:100)

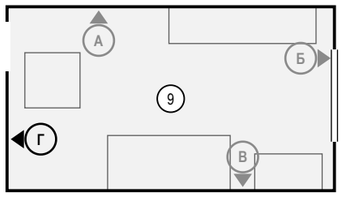

Ведомость изделий и проёмов (на листе)

Марка	Изделие, проём	На виде Ш×В, мм	Низ, мм
ДК4	зеркало	600×1600	300
Д-2	дверь скрытого монтажа	800×2100	0

Примечания

1. Развёртки — вид на стену изнутри помещения, по часовой стрелке; расположение — на схеме листа и на листе 80; размеры — в мм по чистовым поверхностям; отметки — в м от ±0,000; высоты Н — от чистого пола помещения до оси изделия, у декора — до центра.
2. Красная цепочка — привязки электроточек и выводов по осям от угла чистовых стен; высота Н — у знака, от чистого пола до оси; высоты мебели, проёмов и границ отделки — колонкой отметок слева. У знака — короткая марка; назначение, группа щита, высота и привязка каждой точки и вывода — в «Ведомости точек и выводов» под видами (каждая точка — строка).
3. У знака электроточки: марка (Р — розетка, S — выключатель, Св — светильник, ЭВ — вывод кабеля), ×N — число постов в рамке, гр. — группа щита, Н — высота оси от чистого пола, мм; группы по клавишам выключателя — на листе выключателей.
4. Схема мебели, приборов и декора не является технической документацией для производства мебели; габариты — по паспортам изделий.
5. Картины и зеркала крепить к основанию по паспорту изделия (закладные и анкеры — в перечне скрытых работ); крест — ось центра предмета.
6. Двери скрытого монтажа — полотно в плоскости стены, отделка стены по полотну, плинтус прерывается у короба (узел — на листе узлов).
7. Потолок — у каждой стены свой, по плану потолков (ПТ3); ступени — зоной, кромка короба перед нишей — тонкой линией; в поле потолка: ПТ1 +2,600.

Допущения и предложения на листе

Основа листа: размеры сняты с растрового плана заказчика без размеров: масштаб восстановлен по площадям помещений (≈ 11,8 мм на пиксель), контрольный обмер не выполнен (К-1); высота потолка 2700 мм принята: на плане заказчика её нет (К-2); толщины стен 300 / 120 мм приняты по плану заказчика, не замерены (К-1); разрешённая мощность 15 кВт принята по типовым ТУ для квартиры, ТУ заказчиком не переданы (К-4); подрайон климата не задан — принят не северный (жилые от 2,5 м) (К-9).
См. лист открытых вопросов (лист 6, записи К-1, К-2, К-4; лист 7, запись К-9).

1000 мм · печать 1:1

Изм.	Кол.уч	Лист	№ док.	Подп.	Дата
Разраб.		Кырлан А.С.			14.11.26
Пров.					
ГИП					
Н. контр.					
Утв.					

ГД-2026-007-АИ

Квартира 65 м²

Общая площадь 65,24* м² · * размеры со скана, не замерены (реестр — л. 6–8, К-1)

Дизайн-проект интерьера

Стадия	Лист	Листов
РП	102	117

Развёртка стены Г. Детская (пом. 9)

М 1:20

Кырлан Александр Сергеевич


выпуск 14.11.2026 № 9cc0b98f36 · стр. 111 из 139

Узлы

Пороги и стыки покрытий, скрытые двери, короба стояков, гидроизоляция, плинтус

1 Порог 15 мм: мокрая зона — смежное помещение (М 1:5)


Применение: двери Д-5, Д-4; места — лист 80

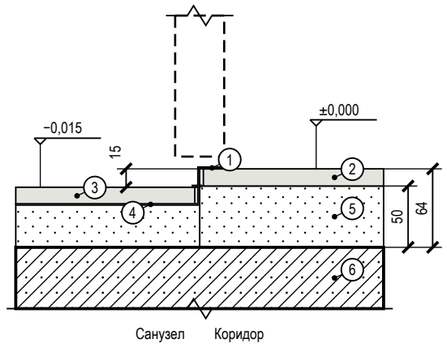

Поз.	Состав слоя, изделие
1	порог-переход металлический, перепад 15 мм, на клей-герметик
2	керамогранит на клею С2 TE S1
3	керамогранит на клею С2 TE S1
4	гидроизоляция в 2 слоя с подъёмом на торец ступени, лента в углу
5	ЦПС М200 50 мм; в мокрой зоне 33 мм
6	плита перекрытия

2 Дверь скрытого монтажа в плоскости стены, плинтус (М 1:5)


Применение: двери Д-3, Д-2, Д-5, Д-4; места — лист 80

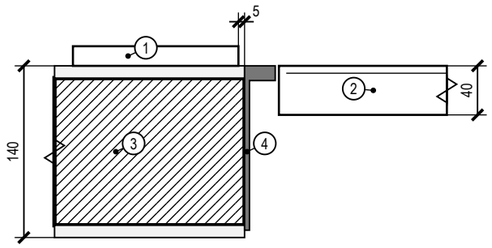

Поз.	Состав слоя, изделие
1	плинтус МДФ 69×16 на клей; у короба — зазор 5 мм, окраска в цвет стены
2	полотно 40 мм под окраску, заподлицо со стеной; теневой шов 3 мм
3	стена 120 мм, штукатурка 10 мм с двух сторон
4	короб скрытого монтажа (алюминий), лицом в плоскости отделки; монтаж до штукатурки

3 Короб стояков К1-1 с люком и звукоизоляцией (М 1:20)


Применение: пом. 6; места — лист 80

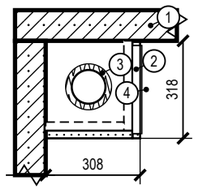

Поз.	Состав слоя, изделие
1	стены существующие — не ослаблять
2	короб: профиль 27×28, ГКЛВ 2×12,5 мм, облицовка плиткой
3	звукоизоляция стояков рулонная 20 мм; К1-1 Ø110
4	ревизионный люк 300×400 мм нажимной, под плитку; против ревизии стояка

4 Гидроизоляция санузла: заход на стены 200 мм, примыкание ванны (М 1:20)


Применение: пом. 6, 7; места — лист 80

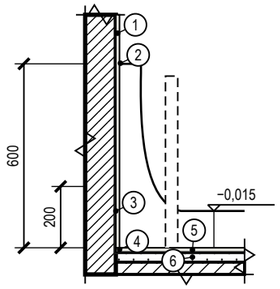

Поз.	Состав слоя, изделие
1	облицовка — плитка на клею С2 TE S1, затирка CG2WA
2	примыкание ванны: лента бордюрная + силиконовый санитарный герметик; облицовка опирается на борт
3	гидроизоляция обмазочная в 2 слоя, заход на стены 200 мм (в зоне душа — выше), до облицовки; акт скрытых работ, тест проливом
4	лента гидроизоляционная в углах и у трапов
5	керамогранит на клею С2 TE S1
6	ЦПС М200 33 мм

5 Плинтус МДФ 69×16 мм у окрашенной стены по доске (ламинату) (М 1:10)


Применение: пом. 1, 2, 3, 8, 9; места — лист 80

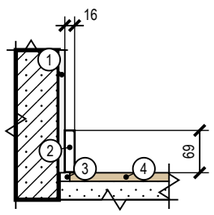

Поз.	Состав слоя, изделие
1	штукатурка, шпаклёвка Q3, окраска — по ведомости отделки
2	плинтус МДФ 69×16 под окраску в цвет стены; клей монтажный — к стене, не к полу
3	зазор покрытия у стены 8–10 мм закрывается плинтусом
4	инженерная доска на клею

6 Плинтус МДФ 69×16 мм у окрашенной стены по керамограниту (плитке) (М 1:10)

Применение: пом. 4, 5; места — лист 80

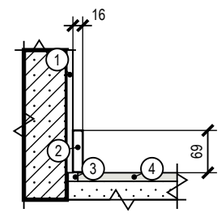

Поз.	Состав слоя, изделие
1	штукатурка, шпаклёвка Q3, окраска — по ведомости отделки
2	плинтус МДФ 69×16 под окраску в цвет стены; клей монтажный — к стене, не к полу
3	зазор покрытия у стены 8–10 мм закрывается плинтусом
4	керамогранит на клею С2 TE S1

Условные обозначения

- железобетон (плита, стены) — условно: конструкция не установлена
- кладка, перегородка — условно: конструкция не установлена
- стяжка, раствор
- гипсокартон ГКЛВ
- звукоизоляция, эластичный заполнитель
- плитка, керамогранит на клею
- инженерная доска (покрытие пола)
- металлический профиль (порог, Т-профиль, короб двери)
- гидроизоляция (обмазочная, лента)

Примечания

1. Узлы — типовые решения проекта для мест, отмеченных выносками на листе схемы расположения развёрток и узлов; размеры — в мм, отметки — в м от ±0,000.
2. Узлы с гидроизоляцией, закладными и коробами скрытого монтажа принимаются по актам скрытых работ до закрытия отделкой; гидроизоляция — после теста проливом (24 ч).
3. Марки изделий (порог, Т-профиль, короб скрытой двери, люк) — по спецификациям; замена — на аналог с теми же габаритами по согласованию с автором проекта.
4. Материал плиты перекрытия и стен в узлах показан условно (железобетон, кладка): конструкция дома не установлена — крепёж, анкеры и толщины слоёв уточняются после обследования (до него — по допущениям общих указаний).

Допущения и предложения на листе. Основа листа: размеры сняты с растрового плана заказчика без размеров: масштаб восстановлен по площадям помещений (≈ 11,8 мм на пиксель), контрольный обмер не выполнен (К-1); высота потолка 2700 мм принята: на плане заказчика её нет (К-2); толщины стен 300 / 120 мм приняты по плану заказчика, не замерены (К-1); разрешённая мощность 15 кВт принята по типовым ТУ для квартиры, ТУ заказчиком не переданы (К-4); подрайон климата не задан — принят не северный (жилые от 2,5 м) (К-9). См. лист открытых вопросов (лист 6, записи К-1, К-2, К-4; лист 7, запись К-9).

Изм.	Кол.уч	Лист	№ док.	Подп.	Дата
Разраб.		Кырлан А.С.			14.11.26
Пров.					
ГИП					
Н. контр.					
Утв.					

ГД-2026-007-АИ

Квартира 65 м²

Общая площадь 65,24* м² · * размеры со скана, не замерены (реестр — л. 6–8, К-1)

Дизайн-проект интерьера

Стадия	Лист	Листов
РП	103	117

Узлы

М 1:5; 1:20; 1:10

Кырлан Александр Сергеевич

выпуск 14.11.2026 № 9cc0b98f36 · стр. 112 из 139

10

Смета

Кырлан Александр Сергеевич

выпуск 14.11.2026 · 9cc0b98f36 · стр. 113 из 139

Ведомость объёмов работ

ПРЕДВАРИТЕЛЬНО · не для производства работ · открыто пунктов: 14 (реестр — л. 6–8)

Объёмы по помещениям от чертежа · площади в м², длины в м · формула, правило проёмов и источник в каждой строке

Ведомость объёмов работ по помещениям

Поз.	Наименование работ (материал, число слоёв)	Ед. изм.	Объём по помещениям (№ по экспликации)									Всего	Формула подсчёта	Правило проёмов	Источник	Цена за ед., ₽	Стоимость, ₽
			1	2	3	4	5	6	7	8	9						
1. Демонтаж и черновые работы																	
1	Демонтаж существующего покрытия пола до основания	м²	4,20	8,27	18,91	4,15	5,51	1,83	3,85	2,50	16,02	65,24	S пом.		л. 21, 22	по КП	
2	Демонтаж существующей отделки стен до основания	м²	21,37	25,14	46,29	16,60	20,60	13,33	19,29	15,65	37,62	215,89	P × H − проёмы	за вычетом проёмов	л. 21, 22	по КП	
3	Демонтаж существующей отделки потолка до основания	м²	4,20	8,27	18,91	4,15	5,51	1,83	3,85	2,50	16,02	65,24	S пом.		л. 21, 22	по КП	
4	Демонтаж существующих дверных блоков	шт	1	1	1	1	4					8	по ведомости проёмов		л. 22, 23	по КП	
5	Демонтаж существующих сантехприборов и электрооборудования (если есть)	компл											по факту на объекте		л. 22	по КП	
6	Монтаж каркасной перегородки П-1: каркас ПС через 600 мм, ГКЛ в 2 слоя с каждой стороны	м²										4,72	1,75 × 2,70 = 4,72 м², одна сторона; пом.	проёмы вычтены	л. 22; схема каркаса перегородки	1 500	7 080
7	Заполнение каркаса П-1 минераловатной плитой (звукоизоляция, Rw — дБ)	м²										4,72	4,72 м² без проёма		схема каркаса перегородки	по КП	
8	Устройство стяжки: стяжка ЦПС М200, 50 мм	м²	4,24	8,35	19,00	4,36	5,80	1,86	3,89	2,54	16,07	66,11	S пом. + S в дверных проёмах (b × t/2)	проёмы добавлены	л. 56, 57	530	35 038
9	Гидроизоляция обмазочная, 2 слоя: пол, стены на 200 мм, зоны замачивания	м²						2,83	5,30			8,13	пол + (P − двери) × h заведения + зоны замачивания		л. 52	450	3 659
10	Штукатурка стен по маякам, до 10 мм	м²	21,37								37,62	58,99	P × H − проёмы по обводу коробок − грани перегородок на ГКЛВ	за вычетом проёмов	л. 21, 57	530	31 265
11	Штукатурка оконных откосов шириной более 200 мм	м²		1,06	1,86						1,08	4,00	Σ (2h + b) × глубина откоса	откосы > 200 мм	л. 21	540	2 160
12	Потолок ГКЛ по каркасу П113, 1 слой	м²		8,27	18,91	4,15	5,51	1,83	3,85		16,02	58,54	S пом. по плану потолков		л. 49–51	1 500	87 810
Итого по разделу 1 — 167 012 ₽ (позиций 12, из них по КП 6); в сводную смету — л. 109, 110																	
2. Инженерные системы																	
13	Прокладка слаботочной линии: Кабель домофона — тип по системе поставщика, отдельно от силовых	м										3,10	по лучам от ЩС**: 1 точ., запас 10 %		л. 36	по КП	
14	Прокладка слаботочной линии: Кабель коаксиальный RG-6 (75 Ом) к розеткам ТВ, отдельно от силовых	м										30,20	по лучам от ЩС**: 2 точ., запас 10 %		л. 36	по КП	
15	Прокладка слаботочной линии: Кабель U/UTP кат. 5e (LAN, Wi-Fi и камеры по PoE), отдельно от силовых	м										42,70	по лучам от ЩС**: 3 точ., запас 10 %		л. 36	по КП	
16	Прокладка слаботочной линии: Кабель U/UTP кат. 6 (LAN, Wi-Fi и камеры по PoE), отдельно от силовых	м										14,20	по лучам от ЩС**: 1 точ., запас 10 %		л. 36	по КП	
17	Прокладка гофротрубы Ø20 для слаботочных линий, отдельно от силовых	м										81,20	по длине лучей без участков в канале плинтуса (≈ 90 %)		л. 36	140	11 368
18	Сборка слаботочного щита ЩС**: корпус, патч-панель, подключение линий и питания 220 В; коммутатор и точки доступа — оборудование заказчика	шт										1	один щит		л. 32, 36	по КП	
19	Электроточка: подрозетник в бетоне, розетка, выключатель, вывод	шт		6	14	2	2		4		11	39	по ведомости электроточек		л. 29, 32	950	37 050
20	Штробы в стенах под спуски кабеля к точкам — выполняются только после технического заключения о несущих стенах	м		12,00	26,55	2,80	4,00		4,86		19,60	69,81	Σ (H − h) по точкам на стенах: вертикальные спуски	после техзаключения	л. 22, 29	по КП	
21	Установка встраиваемого точечного светильника	шт				1	2	1	1		6	11	по плану освещения		л. 30	750	8 250
22	Монтаж светильника: потолочного, подвесного, настенного	шт	1	4	4				1	1	2	13	по плану освещения		л. 30	1 200	15 600

Допущения и предложения на листе

Основа листа: размеры сняты с растрового плана заказчика без размеров: масштаб восстановлен по площадям помещений (≈ 11,8 мм на пиксель), контрольный обмер не выполнен (К-1); высота потолка 2700 мм принята: на плане заказчика её нет (К-2); толщины стен 300 / 120 мм приняты по плану заказчика, не замерены (К-1); разрешённая мощность 15 кВт принята по типовым ТУ для квартиры, ТУ заказчиком не переданы (К-4); подрайон климата не задан — принят не северный (жилые от 2,5 м) (К-9).

Знак «**» — предложение проектировщика, заказчиком не утверждено (согласовать с заказчиком): ЩС — щит слаботочный: место и состав.

См. лист открытых вопросов (лист 6, записи К-1, К-2, К-4; лист 7, запись К-9).

Изм.	Кол.уч	Лист	№ док.	Подп.	Дата
Разраб.		Кырлан А.С.			14.11.26
Пров.					
ГИП					
Н. контр.					
Утв.					

ГД-2026-007-АИ

Квартира 65 м²

Общая площадь 65,24* м² · * размеры со скана, не замерены (реестр — л. 6–8, К-1)

Дизайн-проект интерьера

Стадия	Лист	Листов
РП	104	117

Ведомость объёмов работ

М б/м

Кырлан Александр Сергеевич

Ведомость объёмов работ (продолжение)

ПРЕДВАРИТЕЛЬНО · не для производства работ · открыто пунктов: 14 (реестр — л. 6–8)

Объёмы по помещениям от чертежа · площади в м², длины в м · формула, правило проёмов и источник в каждой строке

Ведомость объёмов работ по помещениям (продолжение)

Поз.	Наименование работ (материал, число слоёв)	Ед. изм.	Объём по помещениям (№ по экспликации)									Всего	Формула подсчёта	Правило проёмов	Источник	Цена за ед., ₽	Стоимость, ₽
			1	2	3	4	5	6	7	8	9						
23	Монтаж LED-ленты в алюминиевый профиль	м			2,50						13,80	16,30	Σ длин лент по плану освещения		л. 30	230	3 749
24	Установка блока питания LED в доступном месте (люк, шкаф)	шт		1	1						1	3	один на LED-группу		л. 30	570	1 710
25	Установка автономного пожарного извещателя	шт		1	1	1	1				1	5	по плану розеток		л. 29	по КП	
26	Сборка щита: установка автоматов и АВДТ групп, вводного автомата	шт										6	группы + вводной автомат		л. 33	230	1 380
27	Установка вводного УЗО	шт										1	по однолинейной схеме		л. 33	380	380
28	Монтаж инсталляции, установка подвесного унитаза и кнопки смыва	шт						1				1	по плану выводов		л. 39, 47	10 500	10 500
29	Короб инсталляции: каркас и обшивка ГКЛВ в 2 слоя, ревизионный доступ к смыву	шт						1	1			2	по плану выводов		л. 39, 52–55	по КП	
30	Короб К1 над чистым полом: каркас и обшивка ГКЛВ под плитку (материалы — в спецификации ВК)	м.п.						1,37	1,24			2,61	Σ открытых участков выпусков К1 (профиль листа разводки ВК)		л. 39, 47	по КП	
31	Установка ванны с сифоном	шт							1			1	по плану выводов		л. 39, 47	6 000	6 000
32	Установка умывальника (мойки) с сифоном и смесителем	шт			1			1	1			3	по плану выводов		л. 39, 47	3 000	9 000
33	Подключение стиральной (посудомоечной) машины к ВК	шт							1			1	по плану выводов		л. 39	по КП	
34	Установка радиатора с узлом подключения и терморегулятором	шт		1	2						1	4	по плану отопления		л. 38	по КП	
Итого по разделу 2 — 104 987 ₽ (позиций 22, из них по КП 11); в сводную смету — л. 109, 110																	
3. Чистовые работы																	
35	Облицовка стен керамогранитом 1200×600 на клею	м²						13,33	19,29			32,62	по раскладке: зона облицовки − место за коробом	за вычетом проёмов	л. 52–55	2 500	81 550
36	Укладка керамогранита на пол, 600×1200, на клею	м²				4,36	5,80	1,86	3,89			15,91	S пом. + S в дверных проёмах	проёмы добавлены	л. 52–56	1 800	28 638
37	Затирка швов керамогранита	м²				4,15	5,51	15,16	23,14			47,96	Σ S облицовки и пола из плитки		л. 52–55	150	7 194
38	Грунтование стен, 2 слоя (под штукатурку и под отделку)	м²	21,37	25,14	46,29	16,60	20,60	13,33	19,29	15,65	37,62	215,89	P × H − проёмы	за вычетом проёмов	л. 57	96	20 725
39	Шпаклёвка стен под окраску, 2 слоя (старт и финиш), уровень Q3	м²	21,37	25,14	46,29	16,60	20,60			15,65	37,62	183,27	P × H − проёмы − фартук	за вычетом проёмов	л. 57	750	137 453
40	Грунтование и шпаклёвка оконных откосов, 2 слоя	м.п.		4,60	8,10						4,70	17,40	Σ (2h + b) по окнам	по окнам	л. 21	300	5 220
41	Грунтование потолка, 2 слоя	м²	4,20	8,27	18,91	4,15	5,51	1,83	3,85	2,50	16,02	65,24	S пом.		л. 57	96	6 263
42	Шпаклёвка потолка под окраску, 2 слоя, уровень Q3	м²	4,20	8,27	18,91	4,15	5,51	1,83	3,85	2,50	16,02	65,24	S пом.		л. 49–51, 57	950	61 978
43	Окраска потолка водно-дисперсионной краской, 2 слоя	м²	4,20	8,27	18,91	4,15	5,51	1,83	3,85	2,50	16,02	65,24	S пом.		л. 57	360	23 486
44	Окраска стен водно-дисперсионной краской, 2 слоя	м²	22,84	30,32	52,16	21,22	30,78			17,12	41,70	216,14	P × H − фартук, проёмы не вычитаются	без вычета проёмов	л. 57	300	64 842
45	Окраска оконных откосов, 2 слоя	м.п.		4,60	8,10						4,70	17,40	Σ (2h + b) по окнам	по окнам	л. 21	120	2 088
46	Укладка инженерной доски на клей	м²	4,24	8,35	19,00					2,54	16,07	50,20	S пом. + S в дверных проёмах	проёмы добавлены	л. 56, 57	1 200	60 240
47	Установка плинтуса МДФ h=69 мм	м.п.	7,76	10,26	18,56	5,96	6,99			5,64	15,88	71,05	P − ширина дверных проёмов		л. 57	450	31 973
48	Окраска плинтуса в тоне V503, 2 слоя	м.п.	7,76	10,26	18,56	5,96	6,99			5,64	15,88	71,05	как плинтус		л. 57	300	21 315
49	Монтаж дверей скрытого монтажа под покраску (поставщик дверей)	шт	1	1	1		4					7	по ведомости проёмов		л. 23	5 250	36 750
50	Входная дверь, поставка с монтажом и откосами	шт										1	по ведомости проёмов		л. 23	по КП	

Допущения и предложения на листе

Основа листа: размеры сняты с растрового плана заказчика без размеров: масштаб восстановлен по площадям помещений (≈ 11,8 мм на пиксель), контрольный обмер не выполнен (К-1); высота потолка 2700 мм принята: на плане заказчика её нет (К-2); толщины стен 300 / 120 мм приняты по плану заказчика, не замерены (К-1); разрешённая мощность 15 кВт принята по типовым ТУ для квартиры, ТУ заказчиком не переданы (К-4); подрайон климата не задан — принят не северный (жилые от 2,5 м) (К-9).

См. лист открытых вопросов (лист 6, записи К-1, К-2, К-4; лист 7, запись К-9).

Изм.	Кол.уч	Лист	№ док.	Подп.	Дата
Разраб.		Кырлан А.С.			14.11.26
Пров.					
ГИП					
Н. контр.					
Утв.					

ГД-2026-007-АИ

Квартира 65 м²

Общая площадь 65,24* м² · * размеры со скана, не замерены (реестр — л. 6–8, К-1)

Дизайн-проект интерьера

Стадия	Лист	Листов
РП	105	117

Ведомость объёмов работ (продолжение)

М б/м

Кырлан Александр Сергеевич

Ведомость объёмов работ (окончание)

ПРЕДВАРИТЕЛЬНО · не для производства работ · открыто пунктов: 14 (реестр — л. 6–8)

Объёмы по помещениям от чертежа · площади в м², длины в м · формула, правило проёмов и источник в каждой строке

Ведомость объёмов работ по помещениям (продолжение)

Поз.	Наименование работ (материал, число слоёв)	Ед. изм.	Объём по помещениям (№ по экспликации)									Всего	Формула подсчёта	Правило проёмов	Источник	Цена за ед., ₽	Стоимость, ₽
			1	2	3	4	5	6	7	8	9						
51	Монтаж телевизора M10 на кронштейн, скрытая прокладка HDMI и питания (штроба, трубка), подключение акустики	шт			1							1	по плану расстановки		л. 77	по КП	
Итого по разделу 3 — 589 715 ₽ (позиций 17, из них по КП 2); в сводную смету — л. 109, 110																	

Ведомость подсчёта площадей по помещениям

№	Помещение	S пола, м²	P, м	H, м	P × H, м²	Проёмы, м²	Стены нетто, м²	В дверных проёмах, м²	Плинтус, м	Откосы, м.п.
1	Гардеробная	4,20	8,46	2,70	22,84	1,47	21,37	0,04	7,76	нет
2	Спальня	8,27	11,66	2,60	30,32	5,18	25,14	0,08	10,26	4,60
3	Кухня-гостиная	18,91	20,06	2,60	52,16	5,87	46,29	0,09	18,56	8,10
4	Прихожая	4,15	8,16	2,60	21,22	4,62	16,60	0,21	5,96	нет
5	Коридор	5,51	11,84	2,60	30,78	10,19	20,60	0,29	6,99	нет
6	Санузел	1,83	5,54	2,62	14,49	1,16	13,33	0,03	нет	нет
7	Ванная	3,85	7,94	2,62	20,76	1,47	19,29	0,04	нет	нет
8	Кладовая	2,50	6,34	2,70	17,12	1,47	15,65	0,04	5,64	нет
9	Детская	16,02	16,68	2,50	41,70	4,08	37,62	0,05	15,88	4,70
	Итого	**65,24**			**251,38**	**35,50**	**215,88**	**0,89**	**71,05**	**17,40**

Реестр контрольных сумм

Показатель	По ВОР	По чертежу	Расхождение	Лист
Σ площадей помещений без летних, м² — общая площадь по экспликации	65,24	65,24	0,0 %	л. 21
Стены под окраску, м² (шпаклёвка) ведомость отделки	183,27	183,26	0,0 %	л. 57
Потолки под окраску, м² — ведомость отделки	65,24	65,24	0,0 %	л. 57
Плинтус, м — ведомость отделки	71,05	71,05	0,0 %	л. 57
Плитка к заказу, шт — ведомость плитки	110	110	0,0 %	л. 52
Гидроизоляция, м² — ведомость материалов плитки	8,13	13,46	-39,6 %	л. 52
Точки ЭОМ, шт — планы ЭОМ (без щитов)	73	74	-1,4 %	л. 29, 30

Примечания

1. Объёмы — от геометрии проекта (та же, что на планах и в ведомости отделки), не от общей площади: P — периметр чистого контура, H — от чистого пола до низа потолка, проёмы — по наружному обводу коробок.
2. Подсчёт по ГЭСН-2001-15 и ГЭСН-2001-11: штукатурка и шпаклёвка стен — за вычетом проёмов; окраска водными составами — без вычета проёмов (п. 2.24); откосы — отдельно, по ширине до 200 и более 200 мм; полы — с площадью в дверных проёмах.
3. Плитка — по раскладке (целые и с подрезкой); короб инсталляции и фартук — отдельными строками, двойного счёта облицовки нет. Материалы, запас и количество к заказу — в спецификации материалов.
4. Цены — ориентир по открытым прайсам Москвы (прайсы собраны 21.09.2026, часть расценок сверена повторно 06.10.2026 и 08.11.2026), не коммерческое предложение; «по КП» — расценки нет, строка в итог не входит.
5. Демонтаж — по плану демонтажа и общим указаниям: покрытия пола, отделка стен и потолков, дверные блоки — до основания; объёмы справочные — по плану демонтажа (расценки в книге нет — «по КП»).
6. Штробы в стенах — только после технического заключения о несущих стенах (общие указания, план обмера и демонтажа): строка «Штробы в стенах» вертикальные спуски кабеля от потолочной трассы к точкам, объём не меньше фактического (горизонтальные трассы — по исполнительной схеме). Расценки штробления в прайсе нет — «по КП», в итог не входит; кабель в штробах стен прокладывается после неё.
7. Слаботочные сети: кабель по лучам от ЩС** 90,20 м (U/UTP, RG-6, домофон — по видам), гофра 81,20 м, щит ЩС** с патч-панелью; розетки RJ45 и ТВ монтируются в строке «Электроточка». Длины те же, что в ведомости изделий электрика (одна модель — lowcurrent-engineer/bom.js); оборудование заказчика (точки доступа, камеры, коммутатор) в спецификацию не входит.
8. Перегородки и облицовки ГКЛ (П-1 — 4,72 м²): площадь одной стороны за вычетом проёмов, из той же модели, по которой выпущена схема каркаса; обшивка, профиль и заполнение — в спецификации материалов. Грани перегородок на ГКЛВ вычтены из штукатурки стен (0,00 м²): штукатурят основание, а не обшивку.
9. Коробы: стояков (нет) и К1 над чистым полом (2,61 м открытых участков; труба К1 вдоль стен 14,54 м в короб не зашивается — она за приборами, в раме инсталляции и в шахтах). В спецификации ВК короб К1 заказывается с запасом 10 % — 2,90 м. Материалы коробов стояков и инсталляции — в спецификации материалов, К1 — в спецификации ВК.

Допущения и предложения на листе

Основа листа: размеры сняты с растрового плана заказчика без размеров: масштаб восстановлен по площадям помещений (≈ 11,8 мм на пиксель), контрольный обмер не выполнен (К-1); высота потолка 2700 мм принята: на плане заказчика её нет (К-2); толщины стен 300 / 120 мм приняты по плану заказчика, не замерены (К-1); разрешённая мощность 15 кВт принята по типовым ТУ для квартиры, ТУ заказчиком не переданы (К-4); подрайон климата не задан — принят не северный (жилые от 2,5 м) (К-9).
Знак «**» — предложение проектировщика, заказчиком не утверждено (согласовать с заказчиком): ЩС — щит слаботочный: место и состав.
См. лист открытых вопросов (лист 6, записи К-1, К-2, К-4; лист 7, запись К-9).

Изм.	Кол.уч	Лист	№ док.	Подп.	Дата	ГД-2026-007-АИ			
						Квартира 65 м²			
						Общая площадь 65,24* м² · * размеры со скана, не замерены (реестр — л. 6–8, К-1)			
Разраб.		Кырлан А.С.			14.11.26	Дизайн-проект интерьера	Стадия	Лист	Листов
Пров.							РП	106	117
ГИП									
Н. контр.						Ведомость объёмов работ (окончание)	Кырлан Александр Сергеевич		
Утв.						М б/м			

выпуск 14.11.2026 № 9cc0b98f36 · стр. 116 из 139

Спецификация материалов

Отделочные материалы: чистое количество, запас, упаковка, к заказу · ГОСТ 21.110-2013

ПРЕДВАРИТЕЛЬНО · не для производства работ · открыто пунктов: 14 (реестр — л. 6–8)

Спецификация материалов (ГОСТ 21.110-2013, форма 1)

Поз.	Наименование и техническая характеристика	Тип, марка, артикул	Код продукции	Поставщик	Ед. изм.	Количество				Масса ед., кг	Примечание
						чистое	запас, %	упаковка	к заказу		
Покрытия полов и облицовка											
1	Инженерная доска (дуб натуральный, рабочий слой 4 мм, эмиссия E1, прямая укладка)	1167-1101			м²	50,21	7	по артикулу	53,80 м²		пом. 1, 2, 3, 8, 9; до целой упаковки; л. 56, 57
2	Клей для паркетной и инженерной доски (эластичный, по ТУ изготовителя доски)	по выбору подрядчика			м²	50,21		ведро по ТУ	по ТУ		расход кг/м² — по ТУ клея; л. 56
3	Керамогранит 600×1200 мм SG501600R	SG501600R			шт	28	10	коробка	32 шт		0 целых + 28 с подрезкой; 15,34 м² по раскладке, к заказу 23,04 м²; пом. 4, 5, 6, 7; л. 52–55
4	Керамогранит 1200×600 мм 610010001195	610010001195			шт	70	10	коробка	78 шт		0 целых + 70 с подрезкой; 32,62 м² по раскладке, к заказу 56,16 м²; пом. 6, 7; л. 52–55
Сухие смеси и гидроизоляция											
5	Клей плиточный цементный класса C2 S1 (ГОСТ Р 56387-2018)	по выбору подрядчика			кг	32,16	10	мешок 25 кг	2 меш.	25	слой 5 мм, 1,20 кг/м² на 1 мм; л. 52
6	Клей плиточный цементный класса C2 (ГОСТ Р 56387-2018)	по выбору подрядчика			кг	245,92	10	мешок 25 кг	11 меш.	25	слой 5 мм, 1,20 кг/м² на 1 мм; л. 52
7	Затирка цементная класса класс не задан, цвет — по колерной карте	по выбору подрядчика			кг	3,34	10	упак. 2 кг	2 упак.	2	расход (a+b)/ab × шов × t × 1,6 кг/м²; л. 52
8	Гидроизоляция обмазочная полимерная, 2 слоя, лента в углах, манжеты на выводах	по выбору подрядчика			м²	8,13	10	ведро по ТУ	по ТУ		пом. 6, 7; расход кг/м² — по ТУ; л. 52
9	Лента демпферная по периметру пола из плитки	по выбору подрядчика			м	24,56	10	рулон	28,00 м		л. 52
10	Смесь цементно-песчаная для стяжки М200 (50 мм, 33 мм)	по выбору подрядчика			м³	3,21	5	мешок по ТУ	по ТУ		S 66,11 м² × толщина; армирование и маяки — по ТУ; л. 56
11	Смесь штукатурная гипсовая для машинного и ручного нанесения по маякам, слой до 10 мм	по выбору подрядчика			м²	58,99	10	мешок по ТУ	по ТУ		пом. 1, 9; расход кг/м² на 1 мм слоя — по ТУ смеси, толщина — по замеру кривизны стен; л. 21, 57
Перегородки и облицовки из ГКЛВ											
12	Лист ГКЛ 12,5 мм, 2500 × 1200 мм: обшивка перегородок и облицовок, 2 слоя на сторону	по выбору подрядчика			м²	18,88	10	лист 3,00 м²	7,00 лист		П-1; площадь стороны × 2 слоя × стороны (проёмы вычтены); л. 22; схема каркаса перегородки
13	Профиль направляющий ПН 100: по потолку и полу, перемычки над проёмами	по выбору подрядчика			м	3,50	10	хлыст 3 м	2 шт		П-1; ПН: шаг и положение стоек — на схеме каркаса; длина стойки равна высоте перегородки, стойки режут между направляющими при монтаже; л. 22; схема каркаса перегородки
14	Профиль стоечный ПС 100: стойки через шаг каркаса и короткие над проёмами	по выбору подрядчика			м	10,80	10	хлыст 3 м	4 шт		П-1; ПС: шаг и положение стоек — на схеме каркаса; длина стойки равна высоте перегородки, стойки режут между направляющими при монтаже; л. 22; схема каркаса перегородки
15	Плита минераловатная звукопоглощающая в полость каркаса, толщина по глубине профиля 100 мм	по выбору подрядчика			м²	4,72	10	упаковка по ТУ	по ТУ		П-1; заполнение принято (К-18): марка и плотность — при закупке; Rw системы нормируют с заполнением; л. 22; схема каркаса перегородки
16	Лента уплотнительная самоклеящаяся под профили по потолку, полу и у примыканий к стенам	по выбору подрядчика			м	3,50	10	рулон по ТУ	4,00 м		П-1; по периметру каркаса: потолок, пол без проёма, крайние стойки у примыканий; л. 22; схема каркаса перегородки
17	Саморезы для ГКЛ по металлу (по слоям обшивки), дюбели для направляющих — по ТУ изготовителя системы	по выбору подрядчика			м²	18,88		упаковка по ТУ	по ТУ		П-1; расход шт/м² и шаг дюбелей — по ТУ системы; считаются от площади обшивки; л. 22; схема каркаса перегородки
Слаботочные сети											
18	Кабель домофона — тип по системе поставщика	по выбору подрядчика			м	3,10		бухта по ТУ	4,00 м		по лучам от ЩС**, 1 точ., запас 10 % уже в длине; л. 36
19	Кабель коаксиальный RG-6 (75 Ом) к розеткам ТВ	по выбору подрядчика			м	30,20		бухта по ТУ	31,00 м		по лучам от ЩС**, 2 точ., запас 10 % уже в длине; л. 36

Допущения и предложения на листе

Основа листа: размеры сняты с растрового плана заказчика без размеров: масштаб восстановлен по площадям помещений (≈ 11,8 мм на пиксель), контрольный обмер не выполнен (К-1); высота потолка 2700 мм принята: на плане заказчика её нет (К-2); толщины стен 300 / 120 мм приняты по плану заказчика, не замерены (К-1); разрешённая мощность 15 кВт принята по типовым ТУ для квартиры, ТУ заказчиком не переданы (К-4); подрайон климата не задан — принят не северный (жилые от 2,5 м) (К-9).

Знак «**» — предложение проектировщика, заказчиком не утверждено (согласовать с заказчиком): ЩС — щит слаботочный: место и состав; пол пом. 1–3, 8, 9 — артикул выбран из каталога: Coswick 1167-1101 (инженерная доска, дуб натуральный, лак, 2100×127 мм); предложение исполнителя — выбор подтверждает автор; цены в каталоге нет, в смете «по КП».

См. лист открытых вопросов (лист 6, записи К-1, К-2, К-4; лист 7, запись К-9).

Изм.	Кол.уч	Лист	№ док.	Подп.	Дата

Разраб.	Кырлан А.С.		14.11.26
Пров.			
ГИП			
Н. контр.			
Утв.			

ГД-2026-007-АИ

Квартира 65 м²

Общая площадь 65,24* м² · * размеры со скана, не замерены (реестр — л. 6–8, К-1)

Дизайн-проект интерьера

Стадия	Лист	Листов
РП	107	117

Спецификация материалов

М б/м

Кырлан Александр Сергеевич

Спецификация материалов (окончание)

Отделочные материалы: чистое количество, запас, упаковка, к заказу · ГОСТ 21.110-2013

Спецификация материалов (ГОСТ 21.110-2013, форма 1) (продолжение)

Поз.	Наименование и техническая характеристика	Тип, марка, артикул	Код продукции	Поставщик	Ед. изм.	Количество				Масса ед., кг	Примечание
						чистое	запас, %	упаковка	к заказу		
20	Кабель U/UTP кат. 5e (LAN, Wi-Fi и камеры по PoE)	по выбору подрядчика			м	42,70		бухта по ТУ	43,00 м		по лучам от ЩС**, 3 точ., запас 10 % уже в длине; л. 36
21	Кабель U/UTP кат. 6 (LAN, Wi-Fi и камеры по PoE)	по выбору подрядчика			м	14,20		бухта по ТУ	15,00 м		по лучам от ЩС**, 1 точ., запас 10 % уже в длине; л. 36
22	Гофротруба Ø20 для слаботочных линий, отдельно от силовых	по выбору подрядчика			м	81,20		бухта по ТУ	82,00 м		по длине лучей без участков в канале плинтуса (≈ 90 %); л. 36
23	Розетка компьютерная RJ45, кат. 6, с рамкой и подрозетником	по выбору подрядчика			шт	4		шт	4 шт		LAN1–LAN4; серия механизмов — как у розеток и выключателей; л. 32, 36
24	Розетка телевизионная (коаксиальная) с рамкой и подрозетником	по выбору подрядчика			шт	2		шт	2 шт		ТВ1, ТВ2; серия механизмов — как у розеток и выключателей; л. 32, 36
25	Трубка или монитор домофона (поставка домофонной организации)	по выбору подрядчика			шт	1		шт	1 шт		ДФ1; серия механизмов — как у розеток и выключателей; л. 32, 36
26	Щит слаботочный ЩС**: корпус, DIN-рейка, розетки 220 В	по выбору подрядчика			шт	1		шт	1 шт		ЩС**; серия механизмов — как у розеток и выключателей; л. 32, 36
27	Патч-панель, портов не менее 4	по выбору подрядчика			шт	1		шт	1 шт		серия механизмов — как у розеток и выключателей; л. 32, 36
Лакокрасочные материалы											
28	Краска интерьерная акриловая, матовая, класс истирания 1	Tikkurila Harmony V503 «Winter»			л	5,13	10	банка 2,7 л	3 банк		21,37 м² × 2 сл. × 0,12 л/м²; пом. 1; л. 57
29	Краска интерьерная акриловая, глубокоматовая, класс истирания 2	Tikkurila Anti-Reflex 2 V503 «Winter»			л	4,85	10	банка 2,7 л	2 банк		20,22 м² × 2 сл. × 0,12 л/м²; пом. 1 (пот.), 9 (пот.); л. 57
30	Краска интерьерная акриловая, глубокоматовая, класс истирания 2	Tikkurila S 1502-Y50R			л	6,03	10	банка 2,7 л	3 банк		25,14 м² × 2 сл. × 0,12 л/м²; пом. 2; л. 57
31	Краска интерьерная водно-дисперсионная, глубокоматовая, класс истирания 2	Tikkurila S 0300-N			л	10,80	10	банка 2,7 л	5 банк		45,02 м² × 2 сл. × 0,12 л/м²; пом. 2 (пот.), 3 (пот.), 4 (пот.), 5 (пот.), 6 (пот.), 7 (пот.), 8 (пот.); л. 57
32	Краска интерьерная акриловая, полуматовая, класс истирания 1	Tikkurila S 1002-Y50R			л	11,11	10	банка 2,7 л	5 банк		46,29 м² × 2 сл. × 0,12 л/м²; пом. 3; л. 57
33	Краска интерьерная акриловая, полуматовая, класс истирания 1	Tikkurila S 1502-Y50R			л	8,93	10	банка 2,7 л	4 банк		37,19 м² × 2 сл. × 0,12 л/м²; пом. 4, 5; л. 57
34	Краска интерьерная акриловая, матовая, класс истирания 2	Tikkurila S 0502-Y			л	3,76	10	банка 2,7 л	2 банк		15,65 м² × 2 сл. × 0,12 л/м²; пом. 8; л. 57
35	Краска интерьерная акриловая, матовая, класс истирания 1	Farrow & Ball Modern Emulsion No. 30 «Hague Blue»			л	3,20	10	банка 2,5 л	2 банк		13,35 м² × 2 сл. × 0,12 л/м²; пом. 9; л. 57
36	Краска интерьерная акриловая, матовая, класс истирания 1	Farrow & Ball Modern Emulsion No. 241 «Skimming Stone»			л	5,82	10	банка 2,5 л	3 банк		24,27 м² × 2 сл. × 0,12 л/м²; пом. 9; л. 57
37	Шпаклёвка финишная полимерная под окраску (стены и потолки, Q3)	по выбору подрядчика			м²	248,51	10	ведро по ТУ	по ТУ		расход кг/м² на слой — по ТУ; л. 57
38	Грунтовка акриловая глубокого проникновения, 2 слоя	по выбору подрядчика			м²	281,13	10	канистра по ТУ	по ТУ		расход л/м² — по ТУ; л. 57
Погонажные изделия и потолки											
39	Плинтус напольный МДФ под покраску, h=69 мм, крепление к стене	SX165			м.п.	71,05	10	хлыст 2,4 м	33 шт		пом. 1, 2, 3, 4, 5, 8, 9; длина хлыста — по артикулу; л. 57
40	Потолок подвесной ГКЛ/ГКЛВ по каркасу Knauf П113: листы, профили, подвесы, лента, шпаклёвка швов	Knauf П113			м²	58,54		комплект	по л. потолков		площадь — по ведомости потолков; число листов, профилей и подвесов — по шагам каркаса на листе потолков; л. 49–51

Примечания

1. Чистое количество — из ведомости объёмов работ и раскладки плитки; запас — отдельной графой (доска — по ведомости отделки, плитка, краска и плинтус — 10 %); «к заказу» — с запасом и кратно упаковке.
2. Плитка — штуками по раскладке, запас на каждую поверхность. Калибр (рабочий размер) и тон — одной партией на помещение, калибр указать при заказе и сверить с раскладкой до укладки.
3. Краска — 0,12 л/м² на слой (середина вилки 0,10–0,15 л/м²) по фактической площади окраски из ведомости отделки; колеровка одной партией.
4. «По ТУ» — расход задаёт производитель выбранного продукта; количество к заказу — после выбора марки.
5. Штукатурная смесь — на ту же площадь, что строка ВОР «Штукатурка стен» (58,99 м²): площадь одна, расход смеси задаёт производитель.
6. Потолки ГКЛ: в этой спецификации — площадь системы П113; число листов, профилей и подвесов — по шагам каркаса на листе потолков (подвесы через 1000, несущие через 500, основные через 1200 мм), схема каркаса не выпущена. Сантехника, светильники и мебель — по своим спецификациям.

Допущения и предложения на листе

Основа листа: размеры сняты с растрового плана заказчика без размеров: масштаб восстановлен по площадям помещений (≈ 11,8 мм на пиксель), контрольный обмер не выполнен (К-1); высота потолка 2700 мм принята: на плане заказчика её нет (К-2); толщины стен 300 / 120 мм приняты по плану заказчика, не замерены (К-1); разрешённая мощность 15 кВт принята по типовым ТУ для квартиры, ТУ заказчиком не переданы (К-4); подрайон климата не задан — принят не северный (жилые от 2,5 м) (К-9).

Знак «**» — предложение проектировщика, заказчиком не утверждено (согласовать с заказчиком): ЩС — щит слаботочный: место и состав; пол пом. 1–3, 8, 9 — артикул выбран из каталога: Coswick 1167-1101 (инженерная доска, дуб натуральный, лак, 2100×127 мм); предложение исполнителя — выбор подтверждает автор; цены в каталоге нет, в смете «по КП». См. лист открытых вопросов (лист 6, записи К-1, К-2, К-4; лист 7, запись К-9).

Изм.	Кол.уч	Лист	№ док.	Подп.	Дата
Разраб.		Кырлан А.С.			14.11.26
Пров.					
ГИП					
Н. контр.					
Утв.					

ГД-2026-007-АИ

Квартира 65 м²

Общая площадь 65,24* м² · * размеры со скана, не замерены (реестр — л. 6–8, К-1)

	Стадия	Лист	Листов
Дизайн-проект интерьера	РП	108	117
Спецификация материалов (окончание) М б/м	**Кырлан Александр Сергеевич**		

Смета ориентировочная

ПРЕДВАРИТЕЛЬНО · не для производства работ · открыто пунктов: 14 (реестр — л. 6–8)

Работы, материалы, оборудование, услуги и резерв · цены — ориентир по открытым прайсам, не коммерческое предложение

Сводная смета (прайсы собраны 21.09.2026, часть расценок сверена повторно 06.10.2026 и 08.11.2026, Москва)

№	Наименование работ, материалов, услуг	Ед. изм.	Кол-во	Цена за ед., ₽	Стоимость, ₽			Чей подряд	Срок поставки, дн.	Основание	Источник цены
					план	факт	разница				
Работы — по ведомости объёмов работ											
1	Демонтаж и черновые работы (без 6 поз. по КП)	раздел	1		167 012			бригада		ВОР, поз. 1–12; л. 104–106	по ВОР
2	Инженерные системы (без 11 поз. по КП)	раздел	1		104 987			бригада		ВОР, поз. 13–34; л. 104–106	по ВОР
3	Чистовые работы (без 2 поз. по КП)	раздел	1		589 715			бригада, поставщик		ВОР, поз. 35–51; л. 104–106	по ВОР
Материалы — по спецификации материалов											
4	Инженерная доска	м²	53,80	4 513	242 799			поставщик		спецификация, поз. 1	Ц7
5	Керамогранит 600×1200, 1200×600 мм	м²	79,20	3 500	277 200			поставщик		спецификация, поз. 3, 4	Ц6
6	Клей плиточный цементный класса C2 S1	меш.	13	1 800	23 400			поставщик		спецификация, поз. 5, 6	Ц7
7	Краска Tikkurila (Harmony, Anti-Reflex 2), банка 2,7 л	банк	24	3 510	84 240			поставщик		спецификация, поз. 28, 29, 30, 31, 32, 33, 34	Ц6
8	Краска Farrow & Ball Modern Emulsion, банка 2,5 л	банк	5	5 800	29 000			поставщик		спецификация, поз. 35, 36	Ц7
9	Плинтус напольный МДФ под покраску	шт	33	368	12 144			поставщик		спецификация, поз. 39	Ц7
10	Прочие материалы с расходом по ТУ (клей для доски, затирка, гидроизоляция, демпферная лента, смесь для стяжки, смесь штукатурная гипсовая для машинного и ручного нанесения по маякам, ГКЛВ перегородок, профиль ПН, профиль ПС, минвата в каркас, лента уплотнительная, крепёж каркаса, кабель слаботочки, гофра слаботочки, изделия слаботочки, шпаклёвка, грунтовка, каркас и ГКЛ потолков)	компл	1	по КП				поставщик		спецификация, поз. 2, 7, 8, 9, 10, 11, 12, 13, 14, 15, 16, 17, 18, 19, 20, 21, 22, 23, 24, 25, 26, 27, 37, 38, 40	
Оборудование и мебель — поставка по спецификациям											
11	Кухонный гарнитур по проекту кухни, изготовление и монтаж (4–8 нед.)	компл	1	по КП				поставщик	не задан; ориентир 4–8 нед. от замера	л. 72–74	
12	Двери скрытого монтажа с коробом под покраску, поставка	шт	7	по КП				поставщик	не задан; ориентир ≈ 30 дн.	л. 23	

Допущения и предложения на листе

Основа листа: размеры сняты с растрового плана заказчика без размеров: масштаб восстановлен по площадям помещений (≈ 11,8 мм на пиксель), контрольный обмер не выполнен (К-1); высота потолка 2700 мм принята: на плане заказчика её нет (К-2); толщины стен 300 / 120 мм приняты по плану заказчика, не замерены (К-1); разрешённая мощность 15 кВт принята по типовым ТУ для квартиры, ТУ заказчиком не переданы (К-4); подрайон климата не задан — принят не северный (жилые от 2,5 м) (К-9).

См. лист открытых вопросов (лист 6, записи К-1, К-2, К-4; лист 7, запись К-9).

Изм.	Кол.уч	Лист	№ док.	Подп.	Дата
Разраб.		Кырлан А.С.			14.11.26
Пров.					
ГИП					
Н. контр.					
Утв.					

ГД-2026-007-АИ

Квартира 65 м²

Общая площадь 65,24* м² · * размеры со скана, не замерены (реестр — л. 6–8, К-1)

Дизайн-проект интерьера

Стадия	Лист	Листов
РП	109	117

Смета ориентировочная

М б/м

Кырлан Александр Сергеевич

Смета ориентировочная (окончание)

ПРЕДВАРИТЕЛЬНО · не для производства работ · открыто пунктов: 14 (реестр — л. 6–8)

Работы, материалы, оборудование, услуги и резерв · цены — ориентир по открытым прайсам, не коммерческое предложение

Сводная смета (прайсы собраны 21.09.2026, часть расценок сверена повторно 06.10.2026 и 08.11.2026, Москва) (продолжение)

№	Наименование работ, материалов, услуг	Ед. изм.	Кол-во	Цена за ед., ₽	Стоимость, ₽			Чей подряд	Срок поставки, дн.	Основание	Источник цены
					план	факт	разница				
13	Оборудование заказчика слаботочных сетей: коммутатор — 1 шт	компл	1	по КП				заказчик		л. 32	
14	Сантехника, светильники, мебель и предметы интерьера	компл	1	по КП				поставщик		л. 47; л. 48; л. 77; л. 26–28	
Прочие работы и услуги											
15	Вынос и вывоз строительного мусора	м³		по факту				бригада		после демонтажа	
16	Подъём материалов на этаж (лифтом или вручную — по договору)	т		по факту				бригада		по массе поставки	
17	Доставка чистовых материалов, 10 % от поставки			10 %	66 878			поставщик		от суммы материалов	
18	Уборка после ремонта	м²	65,24	по факту				бригада		S квартиры	
	Итого работы				**861 714**						
	Итого материалы				**668 783**						
	Итого прочие услуги				**66 878**						
	Резерв на непредвиденные работы и материалы, 15 %				**239 606**						
	ВСЕГО ориентировочно (без оборудования и позиций по КП)				**1 836 981**						

Примечания

1. Смета ориентировочная, не коммерческое предложение: объёмы — из ведомости объёмов работ и спецификации материалов, цены — нижняя граница открытых прайсов Москвы (прайсы собраны 21.09.2026, часть расценок сверена повторно 06.10.2026 и 08.11.2026); перед договором цены подтвердить у подрядчика и поставщиков.
2. Источники цен: Ц1 — Домашний мастерок: прайс на отделочные работы, 2026; Ц2 — Домашний мастерок: прайс на плиточные работы, 2026; Ц3 Домашний мастерок: прайс на электромонтажные работы, 2026; Ц4 — Профи ремонтник: штукатурно-малярные работы; Ц5 — Profi.ru: укладка керамогранита на стены, Москва 2026; Ц6 — knowledge/spec-materials.md, разд. 1 и 3: ориентир по сегментам; Ц7 — Розница Москвы, 09.2026: Лемана ПРО, KGSnab, официальный дилер Farrow & Ball.
3. Повторная сверка с прайсом: 06.10.2026 — перегородка в 2 слоя; 08.11.2026 — гофра слаботочки с затяжкой; остальные расценки — по прайсам, собранным 21.09.2026.
4. В итог не вошли позиции «по КП» и «по факту»: оборудование и мебель, двери, материалы с расходом по ТУ, вывоз мусора, подъём и уборка.
5. Доставка — 10 % от материалов, резерв — 15 % (частный ремонт 10–20 %) отдельными строками, в количествах не спрятаны. Графы «факт» и «разница» заполняются по актам.

Допущения и предложения на листе

Основа листа: размеры сняты с растрового плана заказчика без размеров: масштаб восстановлен по площадям помещений (≈ 11,8 мм на пиксель), контрольный обмер не выполнен (К-1); высота потолка 2700 мм принята: на плане заказчика её нет (К-2); толщины стен 300 / 120 мм приняты по плану заказчика, не замерены (К-1); разрешённая мощность 15 кВт принята по типовым ТУ для квартиры, ТУ заказчиком не переданы (К-4); подрайон климата не задан — принят не северный (жилые от 2,5 м) (К-9).

См. лист открытых вопросов (лист 6, записи К-1, К-2, К-4; лист 7, запись К-9).

Изм.	Кол.уч	Лист	№ док.	Подп.	Дата
Разраб.		Кырлан А.С.			14.11.26
Пров.					
ГИП					
Н. контр.					
Утв.					

ГД-2026-007-АИ

Квартира 65 м²

Общая площадь 65,24* м² · * размеры со скана, не замерены (реестр — л. 6–8, К-1)

Дизайн-проект интерьера

Стадия	Лист	Листов
РП	110	117

Смета ориентировочная (окончание)

М б/м

Кырлан Александр Сергеевич

Смета проекта: этапы, помещения, итог

ПРЕДВАРИТЕЛЬНО · не для производства работ · открыто пунктов: 14 (реестр — л. 6–8)

Весь проект: ремонт, мебель, свет, техника, декор · вилка «от … до …» · позиции «по КП» посчитаны отдельно · цены — ориентир, не оферта

Смета проекта: весь проект по категориям (прайсы собраны 21.09.2026, часть расценок сверена повторно 06.10.2026 и 08.11.2026)

Категория	Позиций	С ценой	По КП	Сумма по позициям с ценой, ₽
Ремонт: работы	51	32	19	861 714
Ремонт: материалы отделки и черновые	35	15	20	668 783
Электрика: кабель, механизмы, щит	34	0	34	
Сантехника: приборы, трубы, арматура	33	0	33	
Доставка и услуги	4	1	3	66 878
Мебель (включая кухню)	21	0	21	
Свет: светильники и ленты	27	0	27	
Техника	3	0	3	
Декор и текстиль	44	0	44	
ИТОГО по позициям с ценой (цены — нижняя граница открытых прайсов)	**252**	**48**	**204**	**1 597 375**
Резерв на непредвиденные работы и материалы, 15 % от ремонта				239 606
ВЕСЬ ПРОЕКТ — вилка «от … до …», ₽				**1 597 375 … 1 836 981**
Позиции «по КП» — цена не названа, в итог НЕ входят: работы — 19; материалы отделки и черновые — 20; электрика: кабель, механизмы, щит — 34; сантехника: приборы, трубы, арматура — 33; доставка и услуги — 3; мебель (включая кухню) — 21; свет: светильники и ленты — 27; техника — 3; декор и текстиль — 44			**204**	**итог выше на их цену**

По этапам

Этап	Поз.	С ценой	Сумма, ₽
Демонтаж и черновые работы (работы)	12	6	167 012
Инженерные системы (работы)	22	11	104 987
Чистовые работы (работы)	17	15	589 715
Черновые материалы (смеси, ГКЛ, гидроизоляция)	17	2	23 400
Электрика: кабель, механизмы, щит, слаботочка	34	0	
Сантехника: приборы, трубы, арматура	33	0	
Чистовые материалы (отделка, двери)	18	13	645 383
Доставка и услуги	4	1	66 878
Резерв на непредвиденное, 15 %	1	1	239 606
Итого ремонт (с резервом)			**1 836 981**

По помещениям

Помещение	Работы, ₽	Материалы, ₽	Всего, ₽
Общее по объекту (без привязки к помещению)	20 208		20 208
1. Гардеробная	61 767	33 829	95 596
2. Спальня	95 361	55 908	151 269
3. Кухня-гостиная	188 453	119 979	308 432
4. Прихожая	50 372	17 903	68 275
5. Коридор	86 657	23 072	109 729
6. Санузел	62 055	111 403	173 458
7. Ванная	90 936	170 456	261 392
8. Кладовая	31 714	21 251	52 965
9. Детская	174 191	114 982	289 173
Доставка и услуги			66 878
Резерв 15 %			239 606
Итого ремонт (с резервом)			**1 836 981**

Допущения и предложения на листе

Основа листа: размеры сняты с растрового плана заказчика без размеров: масштаб восстановлен по площадям помещений (≈ 11,8 мм на пиксель), контрольный обмер не выполнен (К-1); высота потолка 2700 мм принята: на плане заказчика её нет (К-2); толщины стен 300 / 120 мм приняты по плану заказчика, не замерены (К-1); разрешённая мощность 15 кВт принята по типовым ТУ для квартиры, ТУ заказчиком не переданы (К-4); подрайон климата не задан — принят не северный (жилые от 2,5 м) (К-9).

См. лист открытых вопросов (лист 6, записи К-1, К-2, К-4; лист 7, запись К-9).

Изм.	Кол.уч	Лист	№ док.	Подп.	Дата
Разраб.		Кырлан А.С.			14.11.26
Пров.					
ГИП					
Н. контр.					
Утв.					

ГД-2026-007-АИ

Квартира 65 м²

Общая площадь 65,24* м² · * размеры со скана, не замерены (реестр — л. 6–8, К-1)

Дизайн-проект интерьера

Стадия	Лист	Листов
РП	111	117

Смета проекта: этапы, помещения, итог

М б/м

Кырлан Александр Сергеевич

выпуск 14.11.2026 № 9cc0b98f36 · стр. 121 из 139

Смета проекта: этапы, помещения, итог (продолжение)

Весь проект: ремонт, мебель, свет, техника, декор · вилка «от … до …» · позиции «по КП» посчитаны отдельно · цены — ориентир, не оферта

Работы по этапам с расценками (ориентир)

№	Работа	Ед.	Объём	Расценка, ₽	Сумма, ₽	Расценка	Чей подряд
1. Демонтаж и черновые работы — работы, ориентир по открытым прайсам							
1	Демонтаж существующего покрытия пола до основания	м²	65,24	по КП			бригада
2	Демонтаж существующей отделки стен до основания	м²	215,89	по КП			бригада
3	Демонтаж существующей отделки потолка до основания	м²	65,24	по КП			бригада
4	Демонтаж существующих дверных блоков	шт	8,00	по КП			бригада
5	Демонтаж существующих сантехприборов и электрооборудования (если есть)	компл		по КП			бригада
6	Монтаж каркасной перегородки П-1: каркас ПС через 600 мм, ГКЛ в 2 слоя с каждой стороны	м²	4,72	1 500	7 080	Ц1	бригада
7	Заполнение каркаса П-1 минераловатной плитой (звукоизоляция, Rw — дБ)	м²	4,72	по КП			бригада
8	Устройство стяжки: стяжка ЦПС М200, 50 мм	м²	66,11	530	35 038	Ц1	бригада
9	Гидроизоляция обмазочная, 2 слоя: пол, стены на 200 мм, зоны замачивания	м²	8,13	450	3 659	Ц1	бригада
10	Штукатурка стен по маякам, до 10 мм	м²	58,99	530	31 265	Ц1	бригада
11	Штукатурка оконных откосов шириной более 200 мм	м²	4,00	540	2 160	Ц4	бригада
12	Потолок ГКЛ по каркасу П113, 1 слой	м²	58,54	1 500	87 810	Ц1	бригада
2. Инженерные системы — работы, ориентир по открытым прайсам							
13	Прокладка слаботочной линии: Кабель домофона — тип по системе поставщика, отдельно от силовых	м	3,10	по КП			бригада
14	Прокладка слаботочной линии: Кабель коаксиальный RG-6 (75 Ом) к розеткам ТВ, отдельно от силовых	м	30,20	по КП			бригада
15	Прокладка слаботочной линии: Кабель U/UTP кат. 5e (LAN, Wi-Fi и камеры по PoE), отдельно от силовых	м	42,70	по КП			бригада
16	Прокладка слаботочной линии: Кабель U/UTP кат. 6 (LAN, Wi-Fi и камеры по PoE), отдельно от силовых	м	14,20	по КП			бригада
17	Прокладка гофротрубы Ø20 для слаботочных линий, отдельно от силовых	м	81,20	140	11 368	Ц3	бригада
18	Сборка слаботочного щита ЩС**: корпус, патч-панель, подключение линий и питания 220 В; коммутатор и точки доступа — оборудование заказчика	шт	1,00	по КП			бригада
19	Электроточка: подрозетник в бетоне, розетка, выключатель, вывод	шт	39,00	950	37 050	Ц3	бригада
20	Штробы в стенах под спуски кабеля к точкам — выполняются только после технического заключения о несущих стенах	м	69,81	по КП			бригада
21	Установка встраиваемого точечного светильника	шт	11,00	750	8 250	Ц3	бригада
22	Монтаж светильника: потолочного, подвесного, настенного	шт	13,00	1 200	15 600	Ц3	бригада
23	Монтаж LED-ленты в алюминиевый профиль	м	16,30	230	3 749	Ц3	бригада
24	Установка блока питания LED в доступном месте (люк, шкаф)	шт	3,00	570	1 710	Ц3	бригада
25	Установка автономного пожарного извещателя	шт	5,00	по КП			бригада
26	Сборка щита: установка автоматов и АВДТ групп, вводного автомата	шт	6,00	230	1 380	Ц3	бригада
27	Установка вводного УЗО	шт	1,00	380	380	Ц3	бригада
28	Монтаж инсталляции, установка подвесного унитаза и кнопки смыва	шт	1,00	10 500	10 500	Ц1	бригада
29	Короб инсталляции: каркас и обшивка ГКЛВ в 2 слоя, ревизионный доступ к смыву	шт	2,00	по КП			бригада
30	Короб К1 над чистым полом: каркас и обшивка ГКЛВ под плитку (материалы — в спецификации ВК)	м	2,61	по КП			бригада
31	Установка ванны с сифоном	шт	1,00	6 000	6 000	Ц1	бригада

Допущения и предложения на листе

Основа листа: размеры сняты с растрового плана заказчика без размеров: масштаб восстановлен по площадям помещений (≈ 11,8 мм на пиксель), контрольный обмер не выполнен (К-1); высота потолка 2700 мм принята: на плане заказчика её нет (К-2); толщины стен 300 / 120 мм приняты по плану заказчика, не замерены (К-1); разрешённая мощность 15 кВт принята по типовым ТУ для квартиры, ТУ заказчиком не переданы (К-4); подрайон климата не задан — принят не северный (жилые от 2,5 м) (К-9).
Знак «**» — предложение проектировщика, заказчиком не утверждено (согласовать с заказчиком): ЩС — щит слаботочный: место и состав.
См. лист открытых вопросов (лист 6, записи К-1, К-2, К-4; лист 7, запись К-9).

Изм.	Кол.уч	Лист	№ док.	Подп.	Дата
Разраб.		Кырлан А.С.			14.11.26
Пров.					
ГИП					
Н. контр.					
Утв.					

ГД-2026-007-АИ

Квартира 65 м²

Общая площадь 65,24* м² · * размеры со скана, не замерены (реестр — л. 6–8, К-1)

Дизайн-проект интерьера

Стадия	Лист	Листов
РП	112	117

Смета проекта: этапы, помещения, итог (продолжение)
М б/м

Кырлан Александр Сергеевич

Смета проекта: этапы, помещения, итог (окончание)

Весь проект: ремонт, мебель, свет, техника, декор · вилка «от … до …» · позиции «по КП» посчитаны отдельно · цены — ориентир, не оферта

Работы по этапам с расценками (ориентир) (продолжение)

№	Работа	Ед.	Объём	Расценка, ₽	Сумма, ₽	Расценка	Чей подряд
32	Установка умывальника (мойки) с сифоном и смесителем	шт	3,00	3 000	9 000	Ц1	бригада
33	Подключение стиральной (посудомоечной) машины к ВК	шт	1,00	по КП			бригада
34	Установка радиатора с узлом подключения и терморегулятором	шт	4,00	по КП			бригада
3. Чистовые работы — работы, ориентир по открытым прайсам							
35	Облицовка стен керамогранитом 1200×600 на клею	м²	32,62	2 500	81 550	Ц5	бригада
36	Укладка керамогранита на пол, 600×1200, на клею	м²	15,91	1 800	28 638	Ц2	бригада
37	Затирка швов керамогранита	м²	47,96	150	7 194	Ц2	бригада
38	Грунтование стен, 2 слоя (под штукатурку и под отделку)	м²	215,89	96	20 725	Ц4	бригада
39	Шпаклёвка стен под окраску, 2 слоя (старт и финиш), уровень Q3	м²	183,27	750	137 453	Ц1	бригада
40	Грунтование и шпаклёвка оконных откосов, 2 слоя	м	17,40	300	5 220	Ц4	бригада
41	Грунтование потолка, 2 слоя	м²	65,24	96	6 263	Ц4	бригада
42	Шпаклёвка потолка под окраску, 2 слоя, уровень Q3	м²	65,24	950	61 978	Ц1	бригада
43	Окраска потолка водно-дисперсионной краской, 2 слоя	м²	65,24	360	23 486	Ц1	бригада
44	Окраска стен водно-дисперсионной краской, 2 слоя	м²	216,14	300	64 842	Ц1	бригада
45	Окраска оконных откосов, 2 слоя	м	17,40	120	2 088	Ц4	бригада
46	Укладка инженерной доски на клей	м²	50,20	1 200	60 240	Ц1	бригада
47	Установка плинтуса МДФ h=69 мм	м	71,05	450	31 973	Ц1	бригада
48	Окраска плинтуса в тоне V503, 2 слоя	м	71,05	300	21 315	Ц1	бригада
49	Монтаж дверей скрытого монтажа под покраску (поставщик дверей)	шт	7,00	5 250	36 750	Ц1	поставщик
50	Входная дверь, поставка с монтажом и откосами	шт	1,00	по КП			поставщик
51	Монтаж телевизора M10 на кронштейн, скрытая прокладка HDMI и питания (штроба, трубка), подключение акустики	шт	1,00	по КП			бригада
4. Прочие работы и услуги — работы, ориентир по открытым прайсам							
52	Кухонный гарнитур по проекту кухни, изготовление и монтаж (4–8 нед.)	компл	1,00	по КП			поставщик
	Итого работы (позиции с расценкой)				**861 714**		

Примечания

1. Итог «ВЕСЬ ПРОЕКТ» — не прогноз, а сумма того, у чего есть цена: ремонт (работы и материалы по смете сметчика), мебель, свет, техника и декор — по ценам из данных проекта. Позиции без цены названы «по КП» (204 шт.) и в итог не входят: пока цена не названа, итог выше напечатанного.
2. Вилка: «от» — сумма по позициям с ценой по нижней границе открытых прайсов (прайсы собраны 21.09.2026, часть расценок сверена повторно 06.10.2026 и 08.11.2026, Москва); «до» — «от» плюс резерв на непредвиденное (15 % от ремонта; частный ремонт 10–20 %).
3. Работы — ориентир по прайсам подрядчиков, не договорная цена: расценку называет бригада после контрольного обмера. Материалы — по «Смете материалов с ценами» (следующий лист).
4. Разбивка по помещениям — доли: общая закупка делится пропорционально площади (длине, числу), по которой считается позиция; работы — по объёму строки в помещении. Сумма по помещениям, по этапам и по категориям одна и та же.
5. Источники расценок и цен: Ц1 — Домашний мастерок: прайс на отделочные работы, 2026; Ц2 — Домашний мастерок: прайс на плиточные работы, 2026; Ц3 — Домашний мастерок: прайс на электромонтажные работы, 2026; Ц4 — Профи ремонтник: штукатурно-малярные работы; Ц5 — Profi.ru: укладка керамогранита на стены, Москва 2026; Ц6 — справочник материалов: ориентир по сегментам; Ц7 — Розница Москвы, 09.2026: Лемана ПРО, KGSnab, официальный дилер Farrow & Ball.
6. Оборудование «по КП» из сметы сметчика (кухня и др.): 1 поз. — в позиции «по КП» мебели и техники.

Допущения и предложения на листе

Основа листа: размеры сняты с растрового плана заказчика без размеров: масштаб восстановлен по площадям помещений (≈ 11,8 мм на пиксель), контрольный обмер не выполнен (К-1); высота потолка 2700 мм принята: на плане заказчика её нет (К-2); толщины стен 300 / 120 мм приняты по плану заказчика, не замерены (К-1); разрешённая мощность 15 кВт принята по типовым ТУ для квартиры, ТУ заказчиком не переданы (К-4); подрайон климата не задан — принят не северный (жилые от 2,5 м) (К-9).
См. лист открытых вопросов (лист 6, записи К-1, К-2, К-4; лист 7, запись К-9).

Изм.	Кол.уч	Лист	№ док.	Подп.	Дата			
Разраб.		Кырлан А.С.			14.11.26	ГД-2026-007-АИ		
Пров.						Квартира 65 м² Общая площадь 65,24* м² · * размеры со скана, не замерены (реестр — л. 6–8, К-1)		
ГИП						Дизайн-проект интерьера	Стадия: РП	Лист: 113 / Листов: 117
Н. контр.						**Смета проекта: этапы, помещения, итог (окончание)** М б/м	**Кырлан Александр Сергеевич**	
Утв.								

Смета материалов с ценами

ПРЕДВАРИТЕЛЬНО · не для производства работ · открыто пунктов: 14 (реестр — л. 6–8)

Все материалы с количеством, запасом, упаковкой, ценой и сроком · цены — ориентир по открытым прайсам, не оферта · работы не входят

Смета материалов с ценами

№	Позиция	Ед.	Нетто	Запас	С запасом	К закупке (упаковка)	Цена за ед., ₽	Сумма, ₽	Заказать заранее	Доп.
Чистовая отделка — позиций 18, с ценой 13, итого 645 383 ₽										
Покрытия полов и облицовка										
1	Инженерная доска (дуб натуральный, рабочий слой 4 мм, эмиссия E1, прямая укладка) — 1167-1101	м²	50,21	7 %	53,72	53,80 м²	4 513 / м²	242 799		8
2	Керамогранит 600×1200 мм SG501600R	шт	28	14 %	32	32 шт · коробка	3 500 / м²	80 640		8
3	Керамогранит 1200×600 мм 610010001195	шт	70	11 %	78	78 шт · коробка	3 500 / м²	196 560		8
Лакокрасочные материалы										
4	Краска интерьерная акриловая, матовая, класс истирания 1 — Tikkurila Harmony V503 «Winter»	л	5,13	10 %	5,64	3 банка · банка 2,7 л	3 510 / банк	10 530		8
5	Краска интерьерная акриловая, глубокоматовая, класс истирания 2 — Tikkurila Anti-Reflex 2 V503 «Winter»	л	4,85	10 %	5,33	2 банка · банка 2,7 л	3 510 / банк	7 020		8
6	Краска интерьерная акриловая, глубокоматовая, класс истирания 2 — Tikkurila S 1502-Y50R	л	6,03	10 %	6,63	3 банка · банка 2,7 л	3 510 / банк	10 530		8
7	Краска интерьерная водно-дисперсионная, глубокоматовая, класс истирания 2 — Tikkurila S 0300-N	л	10,80	10 %	11,88	5 банка · банка 2,7 л	3 510 / банк	17 550		8
8	Краска интерьерная акриловая, полуматовая, класс истирания 1 — Tikkurila S 1002-Y50R	л	11,11	10 %	12,22	5 банка · банка 2,7 л	3 510 / банк	17 550		8
9	Краска интерьерная акриловая, полуматовая, класс истирания 1 — Tikkurila S 1502-Y50R	л	8,93	10 %	9,82	4 банка · банка 2,7 л	3 510 / банк	14 040		8
10	Краска интерьерная акриловая, матовая, класс истирания 2 — Tikkurila S 0502-Y	л	3,76	10 %	4,14	2 банка · банка 2,7 л	3 510 / банк	7 020		8
11	Краска интерьерная акриловая, матовая, класс истирания 1 — Farrow & Ball Modern Emulsion No. 30 «Hague Blue»	л	3,20	10 %	3,52	2 банка · банка 2,5 л	5 800 / банк	11 600		8
12	Краска интерьерная акриловая, матовая, класс истирания 1 — Farrow & Ball Modern Emulsion No. 241 «Skimming Stone»	л	5,82	10 %	6,40	3 банка · банка 2,5 л	5 800 / банк	17 400		8
Погонажные изделия и потолки										
13	Плинтус напольный МДФ под покраску, h=69 мм, крепление к стене — SX165	м	71,05	10 %	78,16	33 шт · хлыст 2,4 м	368 / шт	12 144		8
Двери										
14	Дверь входная Д-1, проём 900×2100 мм	шт	1		1	1 шт	по запросу			6
15	Дверь скрытого монтажа (короб под покраску) Д-2, проём 800×2100 мм, Profil Doors Invisible Скрытая дверь Invisible	шт	2		2	2 шт	по запросу		≈ 30 дн.	6, 7
16	Дверь скрытого монтажа (короб под покраску) Д-3, проём 700×2100 мм, Profil Doors Invisible Скрытая дверь Invisible	шт	3		3	3 шт	по запросу		≈ 30 дн.	6, 7
17	Дверь скрытого монтажа (короб под покраску) Д-4, проём 700×2100 мм, Profil Doors Invisible Скрытая дверь Invisible	шт	1		1	1 шт	по запросу		≈ 30 дн.	6, 7
18	Дверь скрытого монтажа (короб под покраску) Д-5, проём 550×2100 мм, Profil Doors Invisible Скрытая дверь Invisible	шт	1		1	1 шт	по запросу		≈ 30 дн.	6, 7
Черновые материалы — позиций 17, с ценой 2, итого 23 400 ₽										
Покрытия полов и облицовка										
19	Клей для паркетной и инженерной доски (эластичный, по ТУ изготовителя доски)	м²	50,21		50,21	фасовка по ТУ изделия	по запросу			2
Сухие смеси и гидроизоляция										
20	Клей плиточный цементный класса C2 S1 (ГОСТ Р 56387-2018)	кг	32,16	10 %	35,38	2 мешок · мешок 25 кг	1 800 / меш.	3 600		8
21	Клей плиточный цементный класса C2 (ГОСТ Р 56387-2018)	кг	245,92	10 %	270,51	11 мешок · мешок 25 кг	1 800 / меш.	19 800		8
22	Затирка цементная класса класс не задан, цвет — по колерной карте	кг	3,34	10 %	3,67	2 упаковка · упак. 2 кг	по запросу			
23	Гидроизоляция обмазочная полимерная, 2 слоя, лента в углах, манжеты на выводах	м²	8,13	10 %	8,94	фасовка по ТУ изделия	по запросу			2
24	Лента демпферная по периметру пола из плитки	м	24,56	10 %	27,02	28,00 м	по запросу			
25	Смесь цементно-песчаная для стяжки М200 (50 мм, 33 мм)	м³	3,21	5 %	3,37	фасовка по ТУ изделия	по запросу			2

Допущения и предложения на листе

Основа листа: размеры сняты с растрового плана заказчика без размеров: масштаб восстановлен по площадям помещений (≈ 11,8 мм на пиксель), контрольный обмер не выполнен (К-1); высота потолка 2700 мм принята: на плане заказчика её нет (К-2); толщины стен 300 / 120 мм приняты по плану заказчика, не замерены (К-1); разрешённая мощность 15 кВт принята по типовым ТУ для квартиры, ТУ заказчиком не переданы (К-4); подрайон климата не задан — принят не северный (жилые от 2,5 м) (К-9).

Знак «**» — предложение проектировщика, заказчиком не утверждено (согласовать с заказчиком): пол пом. 1–3, 8, 9 — артикул выбран из каталога: Coswick 1167-1101 (инженерная доска, дуб натуральный, лак, 2100×127 мм); предложение исполнителя — выбор подтверждает автор; цены в каталоге нет, в смете «по КП».

См. лист открытых вопросов (лист 6, записи К-1, К-2, К-4; лист 7, запись К-9).

Изм.	Кол.уч	Лист	№ док.	Подп.	Дата
Разраб.		Кырлан А.С.			14.11.26
Пров.					
ГИП					
Н. контр.					
Утв.					

ГД-2026-007-АИ

Квартира 65 м²

Общая площадь 65,24* м² · * размеры со скана, не замерены (реестр — л. 6–8, К-1)

Дизайн-проект интерьера

Стадия	Лист	Листов
РП	114	117

Смета материалов с ценами

М б/м

Кырлан Александр Сергеевич

Смета материалов с ценами (продолжение)

Все материалы с количеством, запасом, упаковкой, ценой и сроком · цены — ориентир по открытым прайсам, не оферта · работы не входят

Смета материалов с ценами (продолжение)

№	Позиция	Ед.	Нетто	Запас	С запасом	К закупке (упаковка)	Цена за ед., ₽	Сумма, ₽	Заказать заранее	Доп.
26	Смесь штукатурная гипсовая для машинного и ручного нанесения по маякам, слой до 10 мм	м²	58,99	10 %	64,89	фасовка по ТУ изделия	по запросу			2
Перегородки и облицовки из ГКЛВ										
27	Лист ГКЛ 12,5 мм, 2500 × 1200 мм: обшивка перегородок и облицовок, 2 слоя на сторону	м²	18,88	10 %	20,77	7 лист · лист 3,00 м²	по запросу			
28	Профиль направляющий ПН 100: по потолку и полу, перемычки над проёмами	м	3,50	10 %	3,85	2 шт · хлыст 3 м	по запросу			
29	Профиль стоечный ПС 100: стойки через шаг каркаса и короткие над проёмами	м	10,80	10 %	11,88	4 шт · хлыст 3 м	по запросу			
30	Плита минераловатная звукопоглощающая в полость каркаса, толщина по глубине профиля 100 мм	м²	4,72	10 %	5,19	фасовка по ТУ изделия	по запросу			2
31	Лента уплотнительная самоклеящаяся под профили по потолку, полу и у примыканий к стенам	м	3,50	10 %	3,85	4,00 м	по запросу			
32	Саморезы для ГКЛ по металлу (по слоям обшивки), дюбели для направляющих — по ТУ изготовителя системы	м²	18,88		18,88	фасовка по ТУ изделия	по запросу			2
Лакокрасочные материалы										
33	Шпаклёвка финишная полимерная под окраску (стены и потолки, Q3)	м²	248,51	10 %	273,36	фасовка по ТУ изделия	по запросу			2
34	Грунтовка акриловая глубокого проникновения, 2 слоя	м²	281,13	10 %	309,24	фасовка по ТУ изделия	по запросу			2
Погонажные изделия и потолки										
35	Потолок подвесной ГКЛ/ГКЛВ по каркасу Knauf П113: листы, профили, подвесы, лента, шпаклёвка швов	м²	58,54		58,54	фасовка по ТУ изделия	по запросу			2
Электрика и слаботочные сети — позиций 34, с ценой 0, итого 0 ₽										
Слаботочные сети										
36	Кабель домофона — тип по системе поставщика	м	3,10		3,10	4,00 м	по запросу			3
37	Кабель коаксиальный RG-6 (75 Ом) к розеткам ТВ	м	30,20		30,20	31,00 м	по запросу			3
38	Кабель U/UTP кат. 5e (LAN, Wi-Fi и камеры по PoE)	м	42,70		42,70	43,00 м	по запросу			3
39	Кабель U/UTP кат. 6 (LAN, Wi-Fi и камеры по PoE)	м	14,20		14,20	15,00 м	по запросу			3
40	Гофротруба Ø20 для слаботочных линий, отдельно от силовых	м	81,20		81,20	82,00 м	по запросу			3
41	Розетка компьютерная RJ45, кат. 6, с рамкой и подрозетником	шт	4		4	4 шт	по запросу			
42	Розетка телевизионная (коаксиальная) с рамкой и подрозетником	шт	2		2	2 шт	по запросу			
43	Трубка или монитор домофона (поставка домофонной организации)	шт	1		1	1 шт	по запросу			
44	Щит слаботочный ЩС**: корпус, DIN-рейка, розетки 220 В	шт	1		1	1 шт	по запросу			
45	Патч-панель, портов не менее 4	шт	1		1	1 шт	по запросу			
Электрика: щит										
46	Автоматический выключатель C10 A, 1P	шт	1		1	1 шт	по запросу			4
47	Автоматический выключатель C16 A, 1P	шт	3		3	3 шт	по запросу			4
48	Автоматический выключатель C32 A, 1P	шт	1		1	1 шт	по запросу			4
49	Корпус щита ЩРВ-П-24, IP41, 24 модулей	шт	1		1	1 шт	по запросу			4
50	Вводной автомат C63, 2P	шт	1		1	1 шт	по запросу			4
51	Вводное УЗО-S 63 A, 100 мА (селективное)	шт	1		1	1 шт	по запросу			4
52	УЗИП тип 2	шт	1		1	1 шт	по запросу			4

Допущения и предложения на листе

Основа листа: размеры сняты с растрового плана заказчика без размеров: масштаб восстановлен по площадям помещений (≈ 11,8 мм на пиксель), контрольный обмер не выполнен (К-1); высота потолка 2700 мм принята: на плане заказчика её нет (К-2); толщины стен 300 / 120 мм приняты по плану заказчика, не замерены (К-1); разрешённая мощность 15 кВт принята по типовым ТУ для квартиры, ТУ заказчиком не переданы (К-4); подрайон климата не задан — принят не северный (жилые от 2,5 м) (К-9).

Знак «**» — предложение проектировщика, заказчиком не утверждено (согласовать с заказчиком): ЩС — щит слаботочный: место и состав; пол пом. 1–3, 8, 9 — артикул выбран из каталога: Coswick 1167-1101 (инженерная доска, дуб натуральный, лак, 2100×127 мм); предложение исполнителя — выбор подтверждает автор; цены в каталоге нет, в смете «по КП».

См. лист открытых вопросов (лист 6, записи К-1, К-2, К-4; лист 7, запись К-9).

Изм.	Кол.уч	Лист	№ док.	Подп.	Дата
Разраб.		Кырлан А.С.			14.11.26
Пров.					
ГИП					
Н. контр.					
Утв.					

ГД-2026-007-АИ

Квартира 65 м²

Общая площадь 65,24* м² · * размеры со скана, не замерены (реестр — л. 6–8, К-1)

Дизайн-проект интерьера

Стадия	Лист	Листов
РП	115	117

Смета материалов с ценами (продолжение)

М б/м

Кырлан Александр Сергеевич

Смета материалов с ценами (продолжение)

Все материалы с количеством, запасом, упаковкой, ценой и сроком · цены — ориентир по открытым прайсам, не оферта · работы не входят

Смета материалов с ценами (продолжение)

№	Позиция	Ед.	Нетто	Запас	С запасом	К закупке (упаковка)	Цена за ед., ₽	Сумма, ₽	Заказать заранее	Доп.
Электрика: механизмы и изделия										
53	Розетка с з/к и защитными шторками, 16 А	шт	22		22	22 шт	по запросу			4
54	Розетка IP44 с крышкой, 16 А	шт	2		2	2 шт	по запросу			4
55	Выключатель 1-клав.	шт	1		1	1 шт	по запросу			4
56	Выключатель 1-клав. проходной	шт	3		3	3 шт	по запросу			4
57	Выключатель 2-клав.	шт	1		1	1 шт	по запросу			4
58	Выключатель 2-клав. (перекрёстная + проходная)	шт	1		1	1 шт	по запросу			4
59	Выключатель 2-клав. проходной	шт	2		2	2 шт	по запросу			4
60	Рамка 1-постовая	шт	26		26	26 шт	по запросу			4
61	Рамка 2-постовая	шт	3		3	3 шт	по запросу			4
62	Коробка установочная (подрозетник) Ø68	шт	32		32	32 шт	по запросу			4
63	Вывод кабеля под прибор (клеммник)	шт	3		3	3 шт	по запросу			4
64	Вывод кабеля к вентилятору вытяжки	шт	1		1	1 шт	по запросу			4
65	Коробка уравнивания потенциалов КУП	шт	1		1	1 шт	по запросу			4
66	Блок питания LED 24 В, 60 Вт	шт	2		2	2 шт	по запросу			4
67	Блок питания LED 24 В, 200 Вт, дим.	шт	1		1	1 шт	по запросу			4
68	Извещатель дымовой автономный	шт	3		3	3 шт	по запросу			4
69	Извещатель тепловой	шт	2		2	2 шт	по запросу			4
Сантехника — позиций 33, с ценой 0, итого 0 ₽										
Сантехника: санитарные приборы										
70	Ванна встраиваемая акриловая 1650×700 мм, с каркасом, экраном и отверстием слив-перелив — Ravak Classic C541000000	шт	1		1	1 шт	по запросу			5
71	Унитаз подвесной безободковый, с сиденьем микролифт, крепёж и звукоизолирующая прокладка — Jacob Delafon Struktura EDF102-00	шт	1		1	1 шт	по запросу			5
72	Инсталляция для подвесного унитаза: рама высотой 1120 мм, бачок, клавиша смыва (ось клавиши 1050 мм от чистого пола)	шт	1		1	1 шт	по запросу			5, 1
73	Умывальник подвесной 400×300 мм, с отверстием под смеситель и переливом — Roca The Gap 7.3274.7.400.0	шт	1		1	1 шт	по запросу			5
74	Умывальник подвесной 550×450 мм, с отверстием под смеситель и переливом — Roca The Gap 7.3274.7.400.0	шт	1		1	1 шт	по запросу			5
75	Мойка кухонная 700×480 мм, с переливом — мойка врезная 700×480 в шкафу М6	шт	1		1	1 шт	по запросу			5
76	Полотенцесушитель электрический, IP44, с терморегулятором	шт	1		1	1 шт	по запросу			5, 1
Сантехника: смесители, сифоны и арматура приборов										
77	Смеситель для ванны настенный однорычажный, межосевое 150 мм, с душевым набором (лейка, шланг, держатель)	шт	1		1	1 шт	по запросу			5, 1
78	Смеситель для умывальника однорычажный, с донным клапаном	шт	2		2	2 шт	по запросу			5, 1
79	Смеситель кухонный однорычажный, высокий излив	шт	1		1	1 шт	по запросу			5, 1
80	Обвязка ванны слив-перелив Ø40/50 с сифоном	шт	1		1	1 шт	по запросу			5, 1
81	Сифон для умывальника бутылочный Ø32/40–50, с гофрой к выпуску	шт	2		2	2 шт	по запросу			5, 1

Допущения и предложения на листе

Основа листа: размеры сняты с растрового плана заказчика без размеров: масштаб восстановлен по площадям помещений (≈ 11,8 мм на пиксель), контрольный обмер не выполнен (К-1); высота потолка 2700 мм принята: на плане заказчика её нет (К-2); толщины стен 300 / 120 мм приняты по плану заказчика, не замерены (К-1); разрешённая мощность 15 кВт принята по типовым ТУ для квартиры, ТУ заказчиком не переданы (К-4); подрайон климата не задан — принят не северный (жилые от 2,5 м) (К-9).

Знак «**» — предложение проектировщика, заказчиком не утверждено (согласовать с заказчиком): пол пом. 1–3, 8, 9 — артикул выбран из каталога: Coswick 1167-1101 (инженерная доска, дуб натуральный, лак, 2100×127 мм); предложение исполнителя — выбор подтверждает автор; цены в каталоге нет, в смете «по КП».

См. лист открытых вопросов (лист 6, записи К-1, К-2, К-4; лист 7, запись К-9).

Изм.	Кол.уч	Лист	№ док.	Подп.	Дата
Разраб.		Кырлан А.С.			14.11.26
Пров.					
ГИП					
Н. контр.					
Утв.					

ГД-2026-007-АИ

Квартира 65 м²

Общая площадь 65,24* м² · * размеры со скана, не замерены (реестр — л. 6–8, К-1)

Дизайн-проект интерьера

Стадия	Лист	Листов
РП	116	117

Смета материалов с ценами (продолжение)

М б/м

Кырлан Александр Сергеевич

Смета материалов с ценами (окончание)

ПРЕДВАРИТЕЛЬНО · не для производства работ · открыто пунктов: 14 (реестр — л. 6–8)

Все материалы с количеством, запасом, упаковкой, ценой и сроком · цены — ориентир по открытым прайсам, не оферта · работы не входят

Смета материалов с ценами (продолжение)

№	Позиция	Ед.	Нетто	Запас	С запасом	К закупке (упаковка)	Цена за ед., ₽	Сумма, ₽	Заказать заранее	Доп.
82	Сифон для мойки Ø40/50	шт	1		1	1 шт	по запросу			5, 1
83	Сифон для стиральной машины встраиваемый в стену Ø50, с обратным клапаном	шт	1		1	1 шт	по запросу			5, 1
84	Кран угловой ½"×½" с гибкой подводкой 40 см (умывальники, мойка)	шт	6		6	6 шт	по запросу			5, 1
85	Кран шаровой угловой ½"×¾" для подключения стиральной и посудомоечной машины	шт	1		1	1 шт	по запросу			5, 1
Сантехника: трубопроводы										
86	Труба полипропиленовая PP-R PN20 Ø20×3,4 (В1) — ГОСТ 32415-2013	м	17,00	10 %	17,00	17,00 м	по запросу			5
87	Труба PP-R, армированная стекловолокном, PN20 Ø20×2,8 (Т3**) — ГОСТ 32415-2013	м	12,00	10 %	12,00	12,00 м	по запросу			5
88	Труба канализационная ПП Ø50 (К1) — ГОСТ 32414-2013	м	13,00	10 %	13,00	13,00 м	по запросу			5
89	Труба канализационная ПП Ø110 (К1) — ГОСТ 32414-2013	м	1,50	10 %	1,50	1,50 м	по запросу			5
Сантехника: фасонные части и выводы										
90	Отвод канализационный ПП 45° Ø50 — ГОСТ 32414-2013	шт	20		20	20 шт	по запросу			5
91	Отвод канализационный ПП 45° Ø110 — ГОСТ 32414-2013	шт	6		6	6 шт	по запросу			5
92	Тройник канализационный ПП 45° (врезки ветвей) — ГОСТ 32414-2013	шт	5		5	5 шт	по запросу			5
93	Ревизия канализационная ПП (после поворота трассы) — ГОСТ 32414-2013	шт	8		8	8 шт	по запросу			5
94	Фитинги PP-R Ø20: тройники, угольники 90° (ветви и повороты В1, Т3**) — ГОСТ 32415-2013	шт	29		29	29 шт	по запросу			5
95	Водорозетка PP-R Ø20×½" настенная, с креплением — ГОСТ 32415-2013	шт	10		10	10 шт	по запросу			5
Сантехника: узлы ввода, люки, короба										
96	Кран шаровой латунный Ду15 PN16 (отключение ввода)	шт	2		2	2 шт	по запросу			5, 1
97	Фильтр сетчатый косой Ду15	шт	2		2	2 шт	по запросу			5, 1
98	Счётчик воды крыльчатый Ду15 (ХВ, ГВ), с поверкой	шт	2		2	2 шт	по запросу			5, 1
99	Клапан обратный Ду15	шт	2		2	2 шт	по запросу			5, 1
100	Люк ревизионный нажимной под плитку 300×400 мм	шт	3		3	3 шт	по запросу			5, 1
101	Звукоизоляция стояка К1 в коробе: рулонный звукоизоляционный материал ≥ 10 мм, обмотка стояка на высоту этажа	м	2,70		2,70	2,70 м	по запросу			5, 1
102	Короб К1 над полом: профиль ПН/ПС, ГКЛВ 12,5 мм под плитку	м	2,90		2,90	2,90 м	по запросу			5, 1
	ИТОГО материалы (позиций с ценой 15 из 102; без цены 87 — «по запросу», в итог не входят)							**668 783**		

Примечания

1. Количества — из единой книги материалов проекта: тот же расход, что в спецификации отделочных материалов, смете и списке покупок. Запас — на подрезку и бой; норма запаса печатается в графе «Запас», её основание — в отдельном документе «Смета на материалы».
2. Цены — нижняя граница открытых прайсов (прайсы собраны 21.09.2026, часть расценок сверена повторно 06.10.2026 и 08.11.2026, Москва); не предложение (оферта) магазинов. Цены нет — «по запросу», позиция в итог не входит. Работы в эту смету не входят (они — на листе «Смета проекта»).
3. Доп. 1. Изделие не выбрано: позиция описана по характеристикам («аналог»); марка, артикул и цена определяются при выборе изделия.
4. Доп. 2. Фасовка не задана в данных: количество дано в мерах расчёта, число упаковок определяется по выбранному продукту (расход и тара — по ТУ).
5. Доп. 3. Длина кабеля — по длинам групп щита из данных электрика; запас на подрезку в длину не заложен — берите бухту с запасом 5–10 %.
6. Доп. 4. Механизмы, рамки и подрозетники — по ведомости изделий электрика; серию механизмов выбирает заказчик.
7. Доп. 5. Трубы и фасонные части — по трассам листа разводки, +10 % на подрезку (уже в количестве); модели приборов заказчик выбирает сам.
8. Доп. 6. Двери: цена и срок называет поставщик после выбора изделия; в смету стоят только если цена задана в данных.
9. Доп. 7. Срок поставки — из данных проекта; если срок не задан, указан типовой диапазон практики как ориентир, а не срок поставщика.
10. Доп. 8. Цена — нижняя граница открытых прайс-листов на дату сбора (книга цен проекта); не коммерческое предложение магазина.
11. Доп. 9. Доли по помещениям справочные: общая закупка делится пропорционально площади (длине, числу), по которой считается позиция.

Допущения и предложения на листе

Основа листа: размеры сняты с растрового плана заказчика без размеров: масштаб восстановлен по площадям помещений (≈ 11,8 мм на пиксель), контрольный обмер не выполнен (К-1); высота потолка 2700 мм принята: на плане заказчика её нет (К-2); толщины стен 300 / 120 мм приняты по плану заказчика, не замерены (К-1); разрешённая мощность 15 кВт принята по типовым ТУ для квартиры, ТУ заказчиком не переданы (К-4); подрайон климата не задан — принят не северный (жилые от 2,5 м) (К-9).
Знак «**» — предложение проектировщика, заказчиком не утверждено (согласовать с заказчиком): пол пом. 1–3, 8, 9 — артикул выбран из каталога: Coswick 1167-1101 (инженерная доска, дуб натуральный, лак, 2100×127 мм); предложение исполнителя — выбор подтверждает автор; цены в каталоге нет, в смете «по КП»; ИЗ-4: Т3.
См. лист открытых вопросов (лист 6, записи К-1, К-2, К-4; лист 7, запись К-9; лист 8, запись ИЗ-4).

Изм.	Кол.уч	Лист	№ док.	Подп.	Дата
Разраб.		Кырлан А.С.			14.11.26
Пров.					
ГИП					
Н. контр.					
Утв.					

ГД-2026-007-АИ

Квартира 65 м²

Общая площадь 65,24* м² · * размеры со скана, не замерены (реестр — л. 6–8, К-1)

Дизайн-проект интерьера	Стадия	Лист	Листов
	РП	117	117

Смета материалов с ценами (окончание)

М б/м

Кырлан Александр Сергеевич

11

Визуализации

Кырлан Александр Сергеевич

выпуск 14.11.2026 № 9cc0b98f36 · стр. 128 из 139



Ванная · общий вид

Квартира 65 м² · визуализация 1 из 11

выпуск 14.11.2026 № 9cc0b98f36 · стр. 129 из 139



Спальня · стена А

Квартира 65 м² · визуализация 2 из 11

выпуск 14.11.2026 № 9cc0b98f36 · стр. 130 из 139

выпуск 14.11.2026 № 9cc0b98f36 · стр. 131 из 139



Спальня · общий вид



Коридор · стена А

Квартира 65 м² · визуализация 4 из 11

выпуск 14.11.2026 № 9cc0b98f36 · стр. 132 из 139



Прихожая · общий вид

выпуск 14.11.2026 № 9cc0b98f36 · стр. 133 из 139



Детская · стена B

Квартира 65 м² · визуализация 6 из 11



Детская · стена Г

Квартира 65 м² · визуализация 7 из 11

выпуск 14.11.2026 № 9cc0b98f36 · стр. 135 из 139

выпуск 14.11.2026 № 9cc0b98f36 · стр. 136 из 139

Кухня-гостиная · стена А

выпуск 14.11.2026 № 9cc0b98f36 · стр. 137 из 139



Кладовая · общий вид



Гардеробная · общий вид

Квартира 65 м² · визуализация 10 из 11

выпуск 14.11.2026 № 9cc0b98f36 · стр. 138 из 139



Санузел · общий вид

Квартира 65 м² · визуализация 11 из 11

выпуск 14.11.2026 № 9cc0b98f36 · стр. 139 из 139