L

LINEA

ДИЗАЙН-ПРОЕКТ ИНТЕРЬЕРА

Квартира 65 м²

Скандинавский

ПАЛИТРА ОТДЕЛКИ

NCS S 1502-Y50	NCS S 1002-Y50	V503	F&B No. 241	NCS S 0502-Y
31 %	23 %	20 %	12 %	8 %

АВТОР ПРОЕКТА

Кырлан Александр Сергеевич

Ноябрь 2026



Визуализация гостиной · 3D

ОБЩАЯ ПЛОЩАДЬ	ПОМЕЩЕНИЙ	СТАДИЯ	ШИФР	ОСНОВА
65,24 м²	9, из них жилых 3	Проект · предварительно	ГД-2026-007-АИ	план заказчика, без обмера

Как оставить правку: кнопка «Правка к этому листу» в правом верхнем углу любого листа · все листы проекта: дизайн-студия-квартир.рф/review.html?p=gost-kv65

выпуск 14.11.2026 № 3aed0ef730 · стр. 1 из 105

Объект

Квартира 65 м²: 65 м², помещений 9, из них жилых 3.

Стиль: скандинавский 100 %. Стадия: предварительный альбом без обмера, планировка по плану заказчика.

Открытых вопросов 12, конфликтов разделов 0; изменений утверждено 3, ждут подписи 2.

Розетки и выводы

24 розетки (рамок 21), 3 вывода кабеля под технику и свет, 5 групп щита — всё с высотами от чистого пола: листы 43, 46.

Что решено (подписано вами)

ИЗ-1 — Диван М-07 у стены А основной части (х 250…2450, у 1650…2600), стол М-05 перед ним (х 1100…2100, у 2800…3800), кресло М-06 у окна 2 (х 400…1150, у 3700…4450).

ИЗ-2 — Диван М-07 — у 1710 мм (было 1700), по чистой грани стены А: х 250…2450, у 1710…2660.

ИЗ-3 — В наружной стене А спальни добавлено окно: смещение от левого угла стены 1400 мм, ширина 1400, высота 1600, подоконник 800 (тот же тип и размеры по высоте, что…

Предложено, ждёт подписи: ИЗ-4, ИЗ-5

Что ждёт вашего ответа

вопросов 12; блокируют заказ или работы — 5, они первыми и выделены

№	Вопрос	Варианты · что будет без ответа	Нужен ответ
К-1	Размеры квартиры сняты с растрового плана заказчика без размерных цепочек: масштаб восстановлен по подписанным площадям помещений.	Без ответа: размеры на листах — по плану заказчика, уточняются по месту; мебель на заказ и материалы по ним не заказывать.	**до заказа мебели и дверей**
К-5	Кухня-гостиная (пом. 3): диван М-07 2200 × 950 стоит в полосе 1400 мм между спальней и кухней — единственном проходе от двери из коридора в комнату.	2026, на утверждение автора): вариант 1 без переноса рабочего места — диван М-07 у стены А основной части (х 250…2450, у 1650…2600), обеденный стол М-05 перед ним (х 1100…2100, у 2800…3800), кресло М-06 у окна 2…	**до заказа мебели и материалов**
К-10	Несущие стены не определены: плана БТИ, проекта дома и технического заключения в материалах объекта нет.	Без ответа: все существующие стены — несущие: перепланировка и штробы в них не выполняются, на листах обмера и демонтажа — «не определены, считать несущими».	**до начала демонтажа и штробления**
К-13	Помещение «Гардеробная»: выключатель основного света L6 (S1) не у входа — у двери Д-3 со стороны ручки свободного места нет (проём в 100 мм от угла, мебель у двери, чужие точки…	Варианты: (а) петли на другую сторону — ручка уходит от угла, выключатель встаёт у ручки; (б) шкаф или тумбу у двери сдвинуть на 300 мм — место освобождается; (в) беспроводной выключатель на клее у ручки (реле в…	**до выпуска рабочей документации**
К-14	Помещение «Коридор»: выключатель основного света L3 (S3, S5) не у входа — у двери А 150, Д-2, Д-2, Д-5, Д-4 со стороны ручки свободного места нет (проём в 100 мм от угла,…	Варианты: (а) петли на другую сторону — ручка уходит от угла, выключатель встаёт у ручки; (б) шкаф или тумбу у двери сдвинуть на 300 мм — место освобождается; (в) беспроводной выключатель на клее у ручки (реле в…	**до выпуска рабочей документации**
К-2	Высота потолка на плане заказчика не указана, принята 2700 мм.	Без ответа: высоты на развёртках и потолки — от 2700 мм, уточнить при обмере.	до выпуска рабочей документации
К-4	Разрешённая мощность квартиры по ТУ неизвестна, принята 15 кВт.	Без ответа: щит и группы рассчитаны на 15 кВт; при меньших ТУ — пересчёт.	до выпуска рабочей документации
К-6	Спальня (пом. 2) без окна: приток не решён — бризер на внутренней стене Б не работает (нужно отверстие в наружной стене), а наружная стена А занята изголовьем кровати…	Без ответа: приток в спальню не обеспечен: на плане вентиляции — «!» в графе притока; радиатор Р-2 — на стене Б.	до выпуска рабочей документации
К-7	Вентканалы на плане заказчика не показаны: ВК-1 и ВК-2 приняты проектировщиком у кухни, ванная (пом. 7) от них далеко — вытяжка ВР3 идёт воздуховодом ≈ 4 м через санузел.	Без ответа: вытяжка ванной — вентилятором с обратным клапаном и воздуховодом под потолком до ВК-2; места решёток до обмера.	до потолков и коробов
К-8	Проём санузла (пом. 6, марка Д-5) по плану заказчика 550×2100 — уже ряда стандартных полотен (600–900): полотно ≈ 450 под заказ, проход меньше 600.	Без ответа: Д-5 — скрытая дверь под заказ по проёму 550×2100 (полотно ≈ 450), проём не расширяется; заказ — только после замера в чистоте.	до заказа дверных блоков
К-9	Климатический подрайон (СП 131.13330) не задан: принят не северный — жилые комнаты и кухня под потолком от 2,5 м (СП 54, п. 5.12).	Без ответа: отметки потолков жилых — по 2,5 м; при северном подрайоне уровни ниже 2,7 м пересчитать до заказа каркаса.	до заказа каркаса потолков
К-12	Циркуляция ГВС в данных не задана — циркуляционного трубопровода на схеме нет.	Без ответа: циркуляции на схеме нет.	до выпуска рабочей документации

Полный текст каждого вопроса, варианты и рекомендация — на листах 81, 82 реестра открытых вопросов.

	Лист	№ док.	Подпись	Дата	Проект: Квартира 65 м²			
Дизайнер	Кырлан А.С.			14.11.26				
Проверил					Ваш проект на одной странице	Стадия	Лист	Листов
Н. контр.								
Утв.						П	2	105



	Лист	№ док.	Подпись	Дата
Дизайнер	Кырлан А.С.			14.11.26
Проверил				
Н. контр.				
Утв.				

Проект: Квартира 65 м²

Визуализация гардеробной	Стадия	Лист	Листов
	П	3	105

выпуск 14.11.2026 № 3aed0ef730 · стр. 3 из 105



	Лист	№ док.	Подпись	Дата	Проект: Квартира 65 м²			
Дизайнер	Кырлан А.С.			14.11.26	Визуализация спальни	Стадия	Лист	Листов
Проверил						П	4	105
Н. контр.								
Утв.								

выпуск 14.11.2026 № 3aed0ef730 · стр. 4 из 105



	Лист	№ док.	Подпись	Дата
Дизайнер	Кырлан А.С.			14.11.26
Проверил				
Н. контр.				
Утв.				

Проект: Квартира 65 м²

Визуализация спальни	Стадия	Лист	Листов
	П	5	105



	Лист	№ док.	Подпись	Дата	Проект: Квартира 65 м²			
Дизайнер	Кырлан А.С.			14.11.26				
Проверил					Визуализация кухни-гостиной	Стадия	Лист	Листов
Н. контр.								
Утв.						П	6	105


выпуск 14.11.2026 № 3aed0ef730 · стр. 6 из 105



	Лист	№ док.	Подпись	Дата
Дизайнер	Кырлан А.С.			14.11.26
Проверил				
Н. контр.				
Утв.				

Проект: Квартира 65 м²

Визуализация прихожей	Стадия	Лист	Листов
	П	7	105

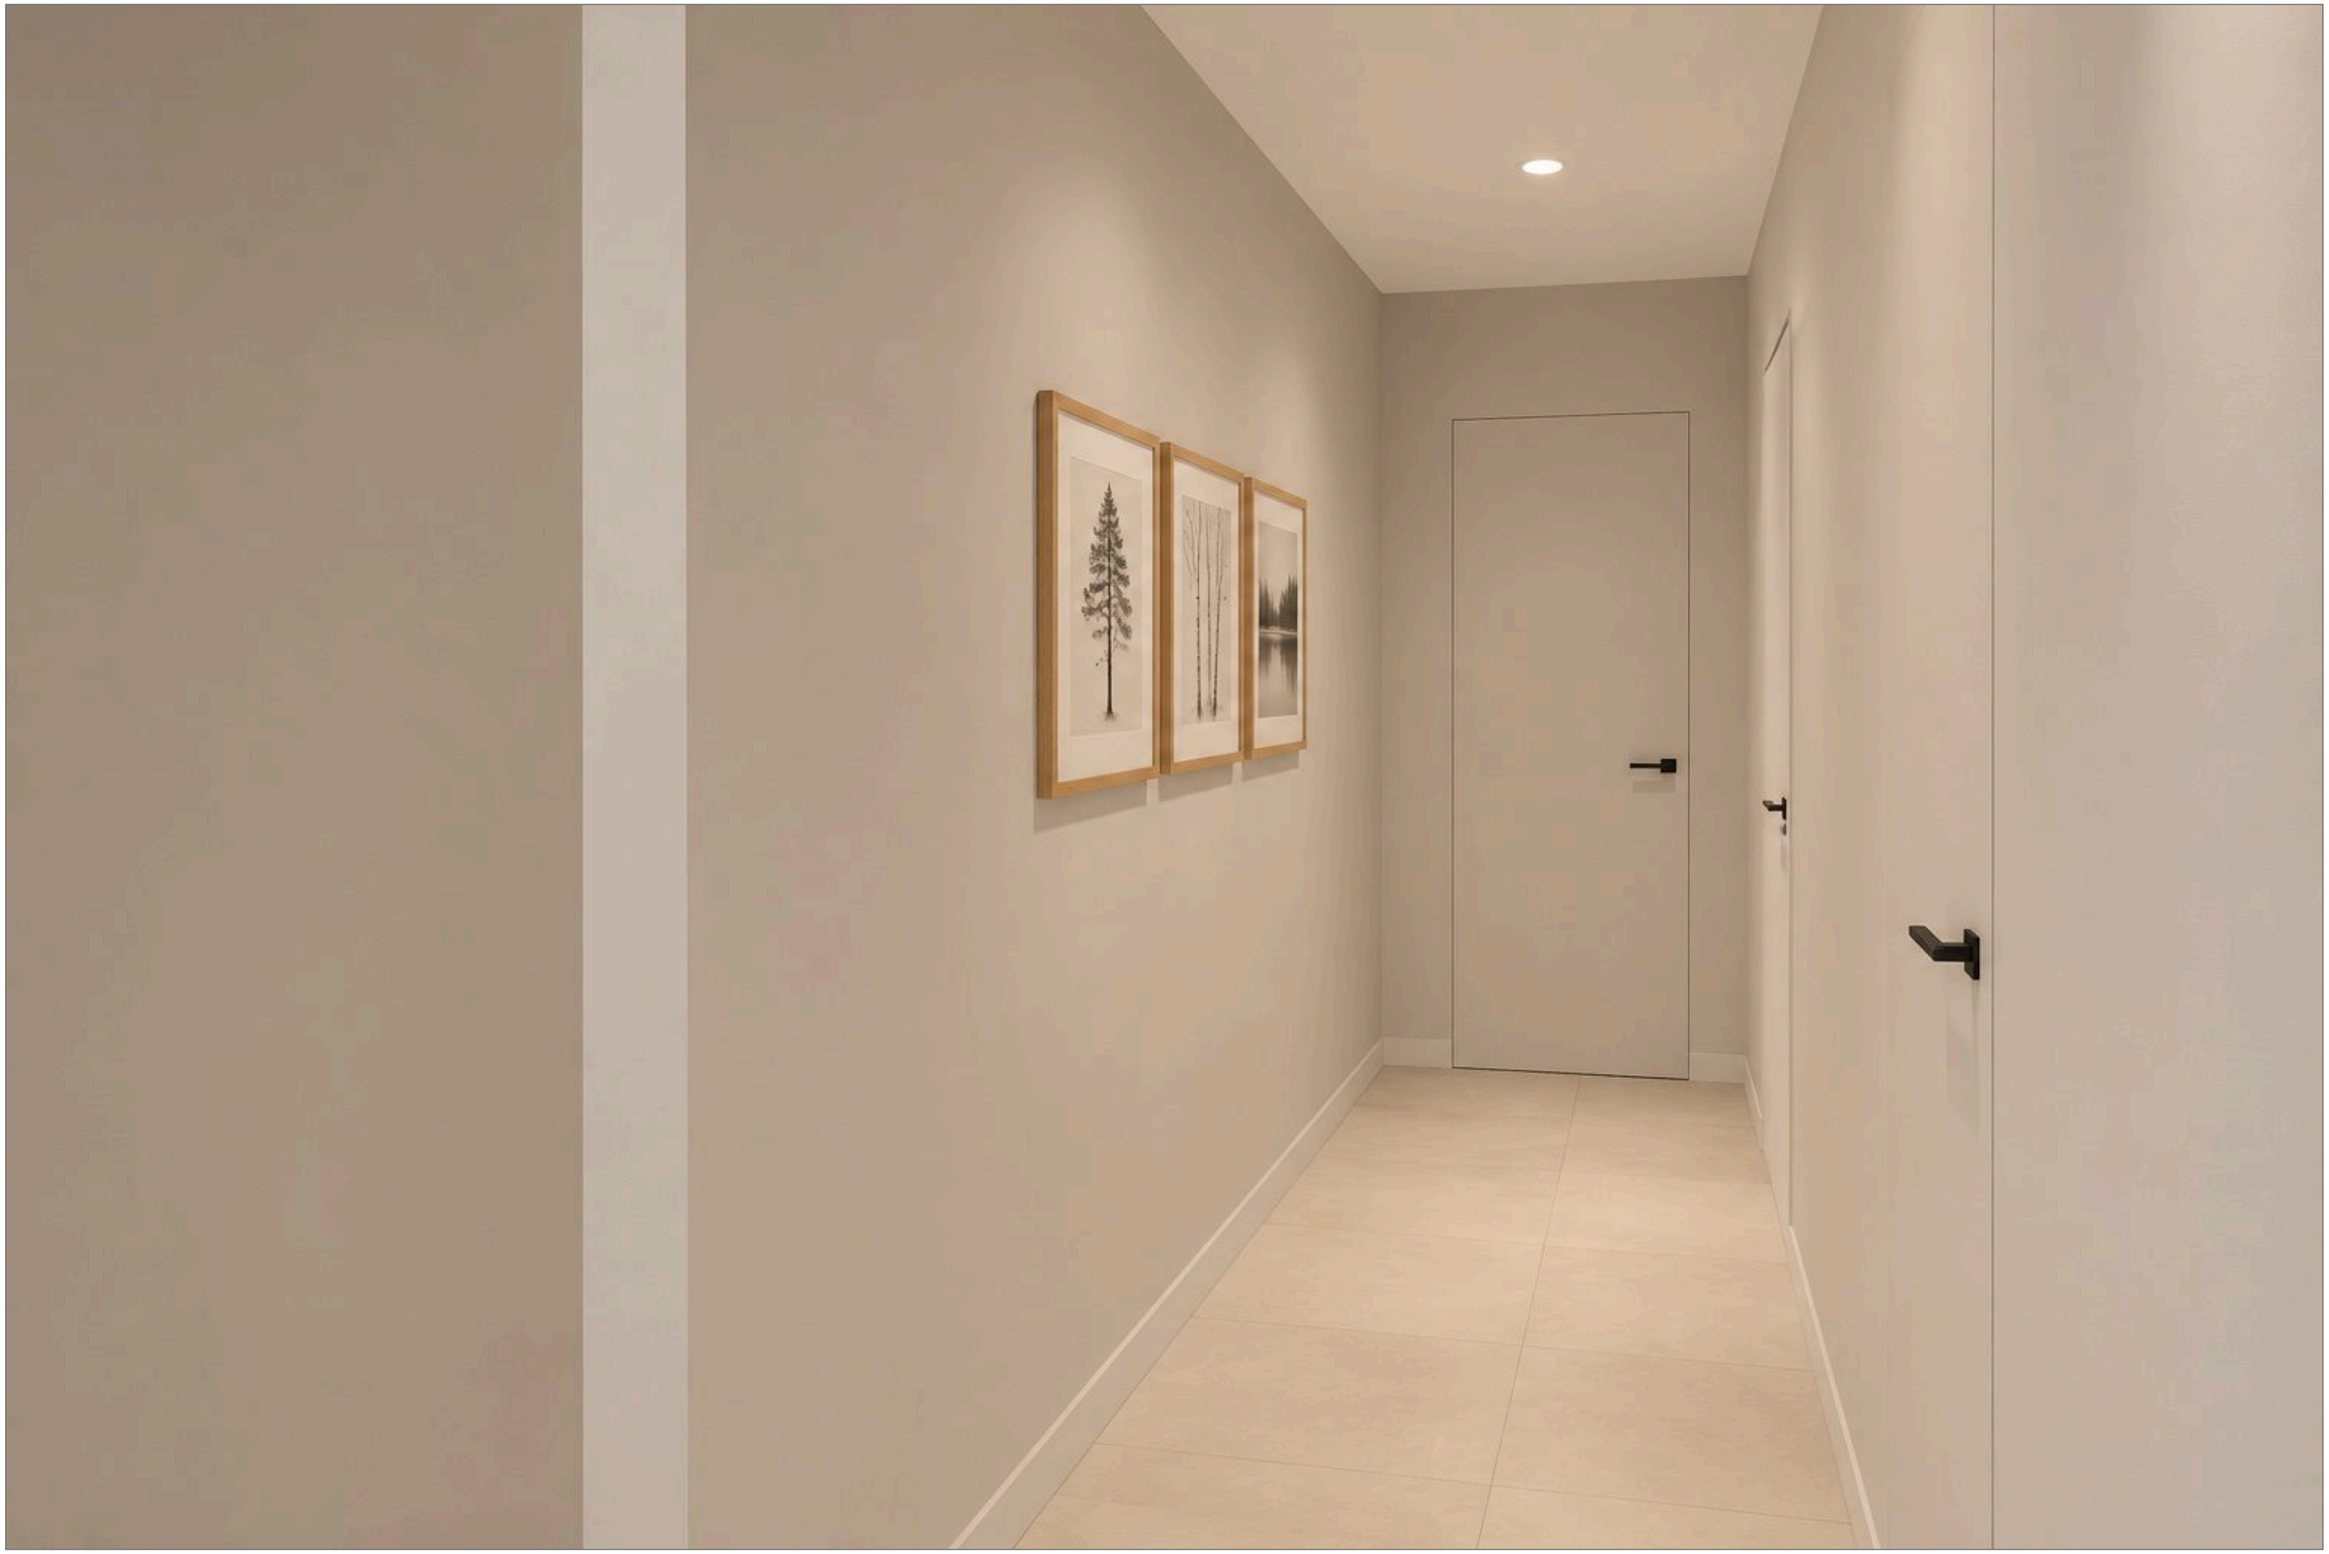

	Лист	№ док.	Подпись	Дата	Проект: Квартира 65 м²			
Дизайнер	Кырлан А.С.			14.11.26	Визуализация коридора	Стадия	Лист	Листов
Проверил						П	8	105
Н. контр.								
Утв.								



	Лист	№ док.	Подпись	Дата	Проект: Квартира 65 м²			
Дизайнер	Кырлан А.С.			14.11.26	Визуализация санузла	Стадия	Лист	Листов
Проверил						П	9	105
Н. контр.								
Утв.								



	Лист	№ док.	Подпись	Дата	Проект: Квартира 65 м²			
Дизайнер	Кырлан А.С.			14.11.26				
Проверил					Визуализация ванной	Стадия	Лист	Листов
Н. контр.								
Утв.						П	10	105

выпуск 14.11.2026 № 3aed0ef730 · стр. 10 из 105



	Лист	№ док.	Подпись	Дата	Проект: Квартира 65 м²			
Дизайнер	Кырлан А.С.			14.11.26				
Проверил					Визуализация кладовой	Стадия	Лист	Листов
Н. контр.								
Утв.						П	11	105



	Лист	№ док.	Подпись	Дата	Проект: Квартира 65 м²			
Дизайнер	Кырлан А.С.			14.11.26				
Проверил					Визуализация детской	Стадия	Лист	Листов
Н. контр.								
Утв.						П	12	105



	Лист	№ док.	Подпись	Дата	Проект: Квартира 65 м²			
Дизайнер	Кырлан А.С.			14.11.26				
Проверил					Визуализация детской	Стадия	Лист	Листов
Н. контр.						П	13	105
Утв.								

выпуск 14.11.2026 № 3aed0ef730 · стр. 13 из 105

Список листов

Лист	Наименование
1	Титульный лист
2	Ваш проект на одной странице
3	Визуализация гардеробной
4	Визуализация спальни
5	Визуализация спальни
6	Визуализация кухни-гостиной
7	Визуализация прихожей
8	Визуализация коридора
9	Визуализация санузла
10	Визуализация ванной
11	Визуализация кладовой
12	Визуализация детской
13	Визуализация детской
14	Список листов
15	Как читать альбом
16	План планировки от заказчика
17	План монтажный
18	Кухня (пом. 3). Монтажная схема
19	Шкафы. Монтажная схема
20	Карта покрытий стен
21	Колерная карта
22	План размещения мебели и оборудования
23	Спецификация мебели и оборудования
24	Спецификация мебели и оборудования (продолжение)
25	Спецификация мебели и оборудования (продолжение)
26	Ведомости изделий, техники и фурнитуры
27	План выводов сантехники
28	Схема разводки водопровода и канализации
29	Аксонометрическая схема В1 (холодное водоснабжение)
30	Аксонометрическая схема Т3 (горячее водоснабжение)
31	Аксонометрическая схема К1 (канализация)
32	Развёртки мокрых зон: выводы ВК. Кухня-гостиная
33	Развёртки мокрых зон: выводы ВК. Санузел
34	Развёртки мокрых зон: выводы ВК. Ванная
35	Спецификация сантехнического оборудования
36	Раскладка плитки. Санузел. Развёртки стен
37	Раскладка плитки. Ванная. Развёртки стен
38	План размещения дверей
39	Ведомость заполнения проёмов
40	План потолков
41	Разрезы и узлы потолков
42	Сечения потолков М 1:10
43	Однолинейная схема щита
44	Таблица нагрузок щита
45	План принципиальных трасс
46	План розеток и электровыводов
47	План слаботочных сетей
48	План освещения
49	Техническое задание на подбор светильников
50	Управление светильниками
51	План вентиляции
52	План отопления
53	План покрытий пола
54	Раскладка плитки. Планы полов
55	Раскладка плитки. Прихожая. Коридор
56	Развёртка стены А. Гардеробная (пом. 1)
57	Развёртки стен Б, Г. Гардеробная (пом. 1)
58	Развёртка стены А. Спальня (пом. 2)
59	Развёртки стен Б, Г. Спальня (пом. 2)
60	Развёртка стены В. Спальня (пом. 2)
61	Развёртка стены В2. Кухня-гостиная (пом. 3), кухонный фронт
62	Развёртка стены Г. Кухня-гостиная (пом. 3), кухонный фронт
63	Развёртка стены А1. Кухня-гостиная (пом. 3)
64	Развёртка стены А2. Кухня-гостиная (пом. 3)
65	Развёртки стен Б1, Б2, В1. Кухня-гостиная (пом. 3)
66	Развёртки стен А, Б. Прихожая (пом. 4)
67	Развёртка стены Г. Прихожая (пом. 4)
68	Развёртка стены А. Коридор (пом. 5)
69	Развёртки стен Б, Г. Коридор (пом. 5)
70	Развёртка стены В. Коридор (пом. 5)
71	Развёртки стен А, Б. Санузел (пом. 6)
72	Развёртки стен В, Г. Санузел (пом. 6)
73	Развёртки стен А, Б. Ванная (пом. 7)
74	Развёртка стены В. Ванная (пом. 7)
75	Развёртка стены Г. Ванная (пом. 7)
76	Развёртки стен. Кладовая (пом. 8)
77	Развёртка стены А. Детская (пом. 9)
78	Развёртка стены Б. Детская (пом. 9)
79	Развёртка стены В. Детская (пом. 9)
80	Развёртка стены Г. Детская (пом. 9)
81	Открытые вопросы, принятые допущения и конфликты. Лист 1 из 2
82	Открытые вопросы, принятые допущения и конфликты. Лист 2 из 2
Д1	Система хранения М-01
Д2	Шкаф-купе М-17
Д3	Система хранения М-18
Д4	Шкаф распашной М-19
Д5	Кухня (пом. 3). Развёртка гарнитура
С1	Ведомость отделки помещений
С2	Спецификация отделочных материалов
С3	Спецификация отделочных материалов
С4	Список покупок
С5	Список покупок (окончание)
С6	Смета проекта: этапы, помещения, итог
С7	Смета проекта: этапы, помещения, итог (продолжение)
С8	Смета проекта: этапы, помещения, итог (окончание)
С9	Смета материалов с ценами
С10	Смета материалов с ценами (продолжение)
С11	Смета материалов с ценами (продолжение)
С12	Смета материалов с ценами (окончание)
С13	Узлы
С14	Календарный график работ и закупок
С15	Чек-лист приёмки по этапам. Лист 1 из 3
С16	Чек-лист приёмки по этапам. Лист 2 из 3
С17	Чек-лист приёмки по этапам. Лист 3 из 3
С18	Лист → мастер

	Лист	№ док.	Подпись	Дата
Дизайнер	Кырлан А.С.			14.11.26
Проверил				
Н. контр.				
Утв.				

Проект: Квартира 65 м²

Список листов	Стадия	Лист	Листов
	П	14	105

выпуск 14.11.2026 № 3aed0ef730 · стр. 14 из 105

Что в альбоме

Альбом — дизайн-проект с рабочими чертежами для ремонта. Листы идут в порядке работ: титул и вводные, реестр открытых вопросов и решений, планы (обмер, монтаж стен, мебель, двери, потолки, полы), инженерия (сантехника, электрика, вентиляция и отопление), развёртки стен с визуализациями помещений, чертежи мебели, ведомости материалов и узлы.

Вам как заказчику — титул, эта вводная, «Ваш проект на одной странице», реестр вопросов, план мебели, визуализации и развёртки, ведомости мебели и материалов. Подрядчику — всё остальное: монтажные планы, привязки выводов и розеток, узлы, ведомости объёмов.

Знаки на листах

Без знака — решение утверждено или подтверждено обмером.

Что проверить до ремонта

1. Розетки у кровати и рабочего места: хватает ли их с каждой стороны кровати и над столом (план розеток — лист 46).

2. Выводы под технику — варочная панель, духовка, посудомойка, стиральная машина, бойлер: совпадают ли с выбранными моделями (листы 23, 24, 25, 46).

3. Высоты розеток, выключателей и выводов даны от чистого пола: если мебель или техника будут другими — скажите до штробления стен.

Номера записей

К-N — открытый вопрос: чего не хватает или что выбрать (варианты и рекомендация — в тексте). Пока ответа нет, действует строка «если решения нет».

Кф-N — конфликт между разделами (например, мебель и радиатор в одном месте); закрывается решением, которое записывается как ИЗ-N.

ИЗ-N — изменение проекта: что было, что стало и кто утвердил. Изменение без подписи предложение.

Все записи — на листе реестра сразу после вводных; на других листах на них стоят ссылки.

Почему альбом предварительный

Обмера на объекте не было: размеры взяты с плана заказчика. Технические условия (мощность, вода, вентиляция дома) не получены, часть решений ждёт вашего ответа. Пока в реестре есть открытые вопросы, альбом предварительный — пометка в штампе снимается закрытием вопросов, а не стиранием.

Правку к любому листу можно оставить по кнопке «Правка к листу» или на сайте студии: дизайн-студия-квартир.рф — укажите номер листа и что изменить.

3 круга правок входят в цену; условия — в договоре и на странице вашего заказа на сайте студии.

Шифр проекта ГД-2026-007-АИ


	Лист	№ док.	Подпись	Дата	Проект: Квартира 65 м²			
Дизайнер	Кырлан А.С.			14.11.26	Как читать альбом	Стадия	Лист	Листов
Проверил						П	15	105
Н. контр.								
Утв.								

Отметки по высоте

±0,000	чистый пол пом. 1–5, 8, 9; отсчёт высот
−0,015	чистый пол пом. 6, 7, ниже на 15 мм
−0,064	верх плиты — расчёт, не замер (задание на обмер)
сущ. пол	снимается до плиты; не замерен (задание на обмер)

Примечания

1. Размеры — в мм по чистым поверхностям стен до отделки (по плану заказчика); площади — в м² по тем же размерам. До начала работ выполнить контрольный обмер.
2. Источник плана: растровый скан плана заказчика, размеры сняты с размерных цепочек, на объекте не замерены.
3. За отметку ±0,000 принят чистый пол, не существующий (блок отметок). «Низ перекрытия» у марки помещения — отметка низа перекрытия от ±0,000, как на развёртках и плане потолков (не высота потолка: потолок — по плану потолков).
4. Толщины стен: наружные 300 мм, перегородки 120 мм; отличающиеся толщины и уступы размерами на плане.
5. Обмер — существующее положение: новых конструкций на листе нет, они — на плане монтажа.
6. Несущие стены не определены: до технического заключения все стены считать несущими; проёмы и штробы в них не выполнять.
7. Дверные проёмы показаны без заполнения (двери — лист 39); высота дверных проёмов 2100 мм, проёмов без двери 2100 мм; низ окон (подоконник) 800 мм от чистого пола, высота окон 1600 мм.
8. Диагонали — контрольные размеры; расхождение более 5 мм подписать на плане как перекос.
9. Размеры проверить на месте до начала работ; расхождение контрольных промеров ≤ 2 %.
10. Размеры короче 1 мм на листе цепочкой не показаны (две выносные линии на таком расстоянии сливаются): пом. 5, стена В — 40 мм от угла до проёма.

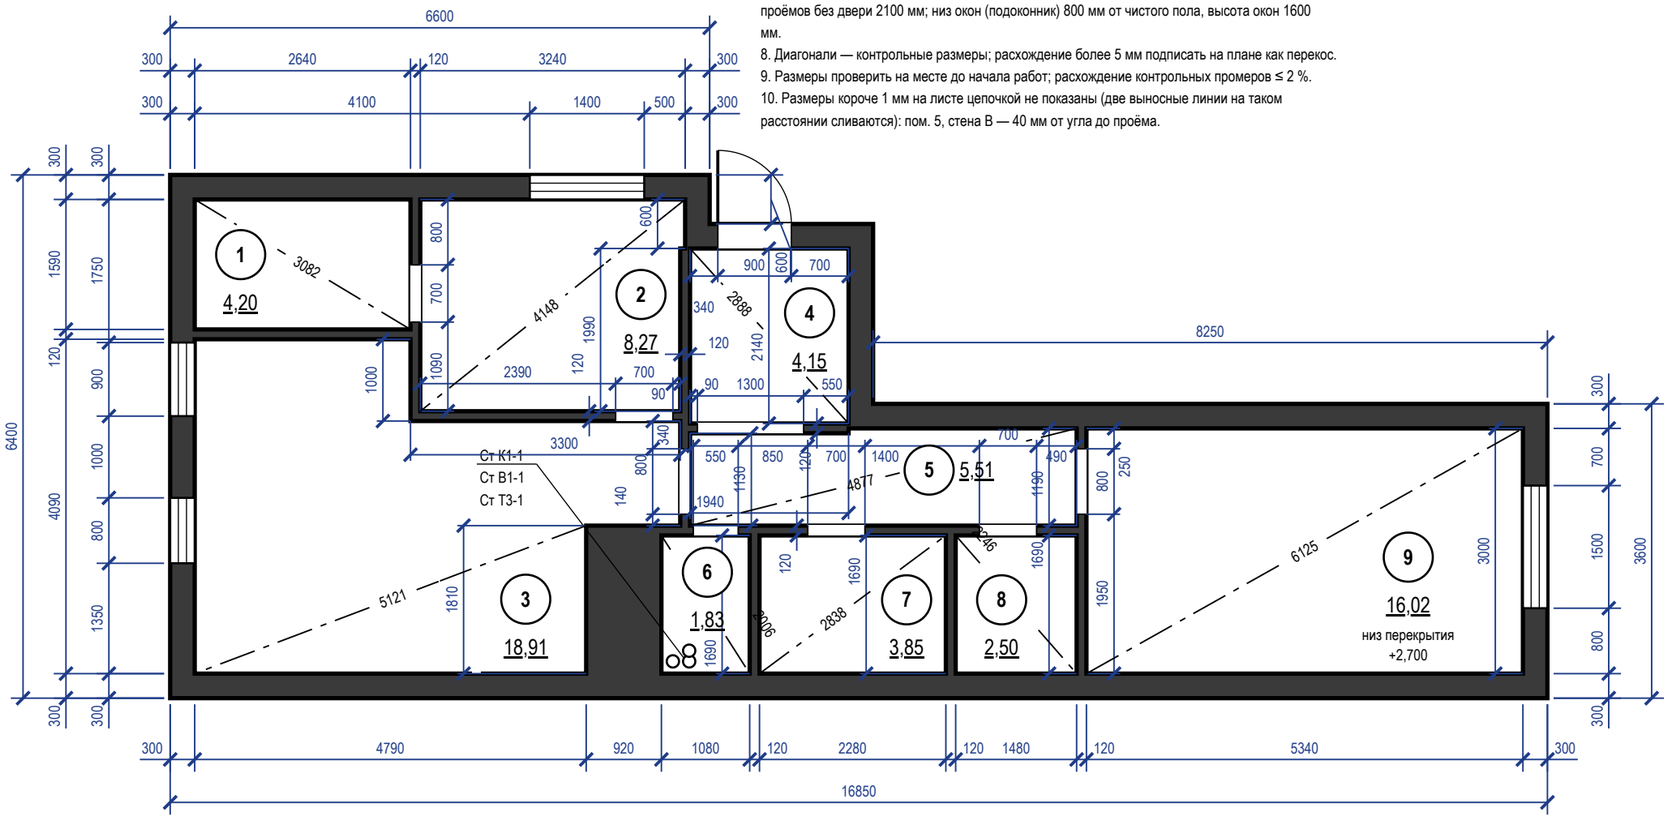


Экспликация помещений

№	Наименование	Площадь, м²
1	Гардеробная	4,20
2	Спальня	8,27
3	Кухня-гостиная	18,91
4	Прихожая	4,15
5	Коридор	5,51
6	Санузел	1,83
7	Ванная	3,85
8	Кладовая	2,50
9	Детская	16,02
	Итого (общая площадь)	**65,24**

Условные обозначения

- существующие стены (сечение)
- окно (рама, остекление)
- проём существующий, без заполнения (откосы)
- стояк: К1 — канализация, В1 — ХВС, Т3 — ГВС
- диагональ помещения — контроль прямоугольности
- (1) номер помещения, площадь м²

	Лист	№ док.	Подпись	Дата	Проект: Квартира 65 м²			М 1:75
Дизайнер	Кырлан А.С.			14.11.26	План планировки от заказчика	Стадия	Лист	Листов
Проверил						П	16	105
Н. контр.								
Утв.								

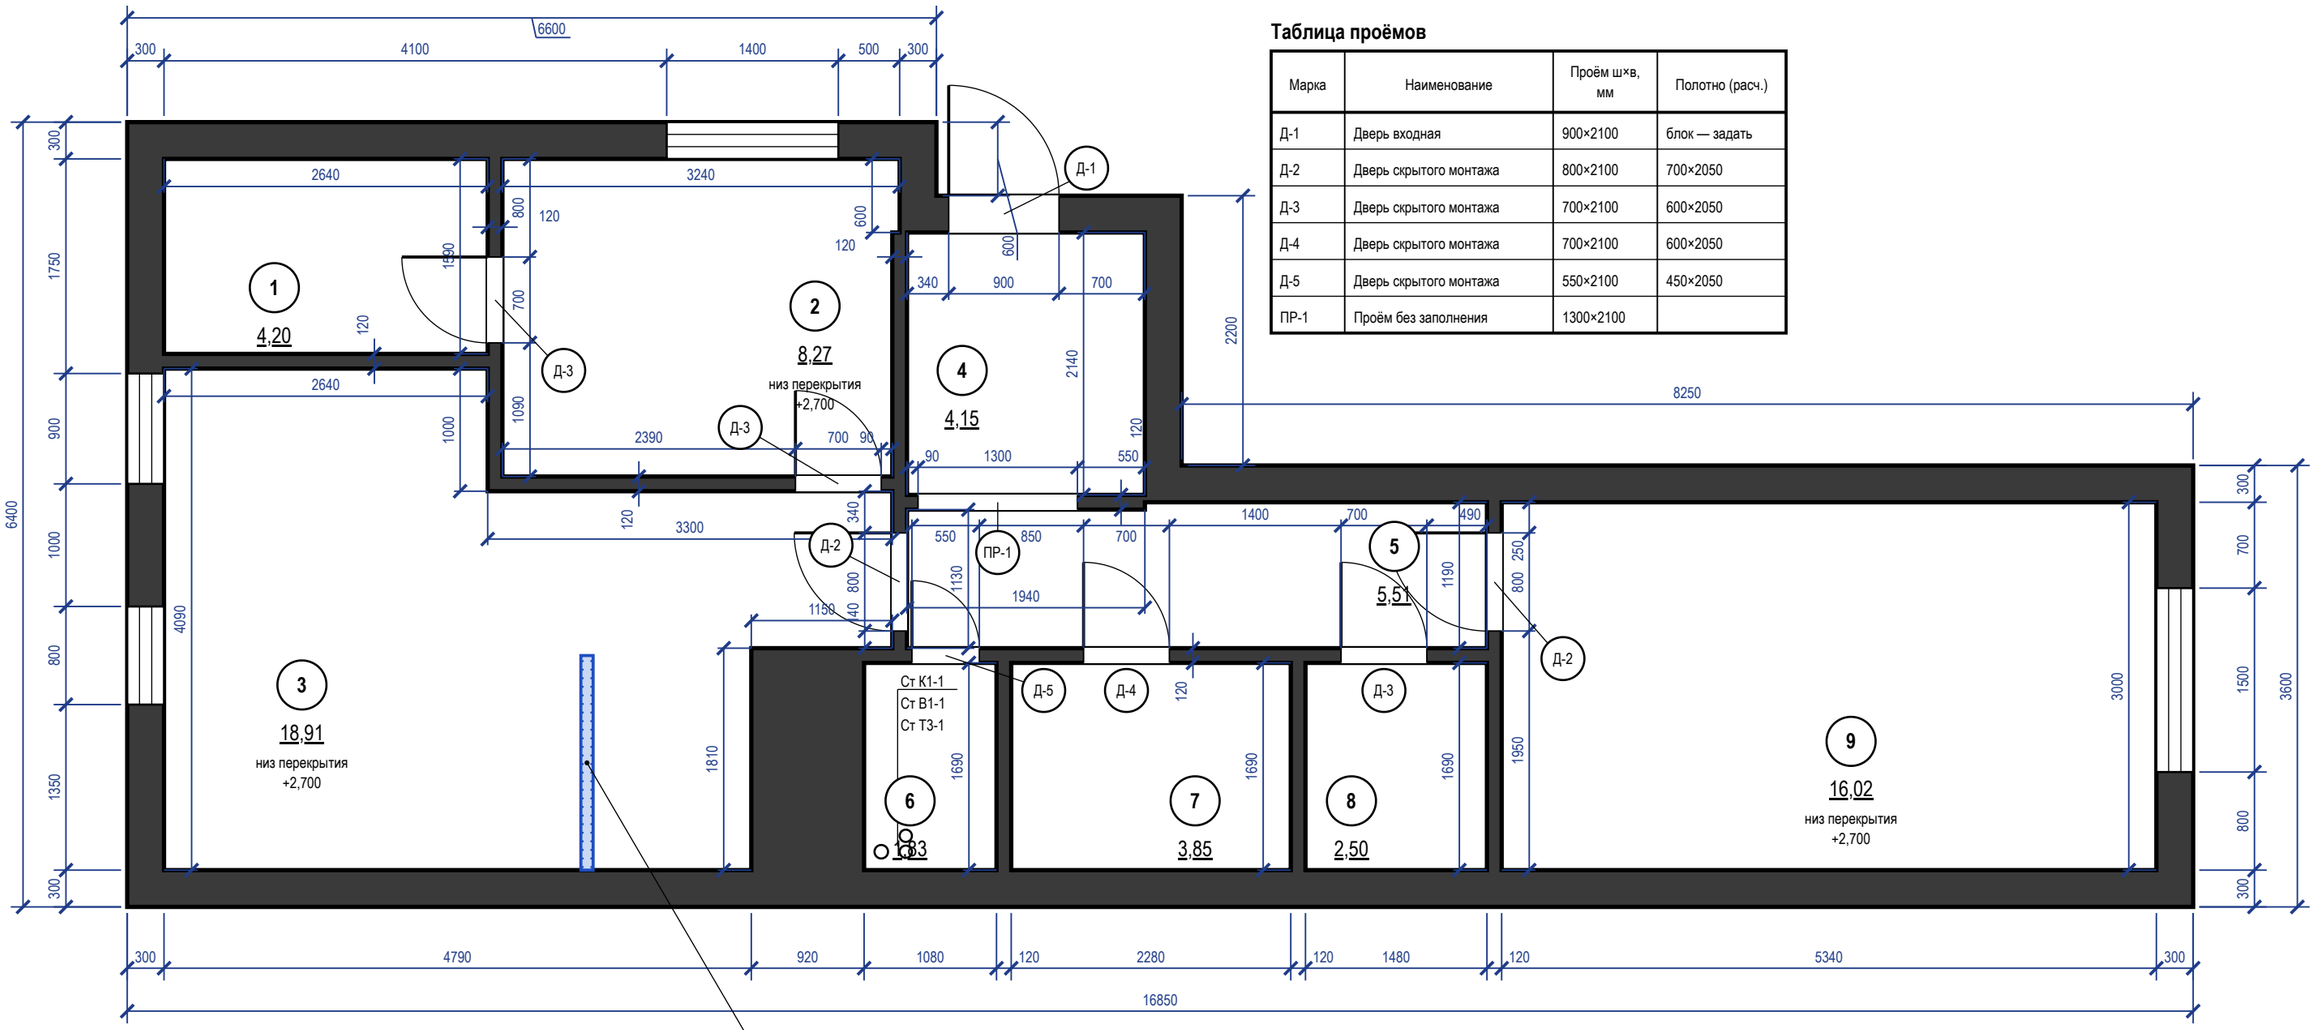

П-1 · перегородка 100 мм, до плиты

ГКЛ 2 слоя с каждой стороны по металлическому каркасу ПС 75

Таблица проёмов

Марка	Наименование	Проём ш×в, мм	Полотно (расч.)
Д-1	Дверь входная	900×2100	блок — задать
Д-2	Дверь скрытого монтажа	800×2100	700×2050
Д-3	Дверь скрытого монтажа	700×2100	600×2050
Д-4	Дверь скрытого монтажа	700×2100	600×2050
Д-5	Дверь скрытого монтажа	550×2100	450×2050
ПР-1	Проём без заполнения	1300×2100	

Экспликация помещений

№	Наименование	Площадь, м²
1	Гардеробная	4,20
2	Спальня	8,27
3	Кухня-гостиная	18,91
4	Прихожая	4,15
5	Коридор	5,51
6	Санузел	1,83
7	Ванная	3,85
8	Кладовая	2,50
9	Детская	16,02
	Итого (общая площадь)	**65,24**

Примечания

1. Размеры — в мм от чистовых поверхностей стен до отделки; размеры уточнить по месту до начала работ.
2. Новые перегородки и облицовки — синим; каркас и обшивка — по выноскам. Д-N, ПР-N в кружке — марка проёма: проём и полотно — по таблице проёмов, «расч.» — полотно по проёму, заказ по выбранной модели; ведомость, отделка и фурнитура — лист 39.
3. Несущие стены не изменять: проёмы, ниши и штробы в них — только по техническому заключению.
4. «расч.» — полотно, выведенное из проёма по запасу каталогов; заказ — по таблице проёмов выбранной модели; Д-1: входной блок по ГОСТ 31173-2016 — задать при выборе блока.
5. Размеры короче 1 мм на листе цепочкой не показаны (две выносные линии на таком расстоянии сливаются): пом. 5, стена В — 40 мм от угла до проёма.

	Лист	№ док.	Подпись	Дата
Дизайнер	Кырлан А.С.			14.11.26
Проверил				
Н. контр.				
Утв.				


Проект: Квартира 65 м² — **М 1:50**

План монтажный


Стадия	Лист	Листов
П	17	105

выпуск 14.11.2026 № 3aed0ef730 · стр. 17 из 105

Привязка выводов и крепление модулей (М 1:20)

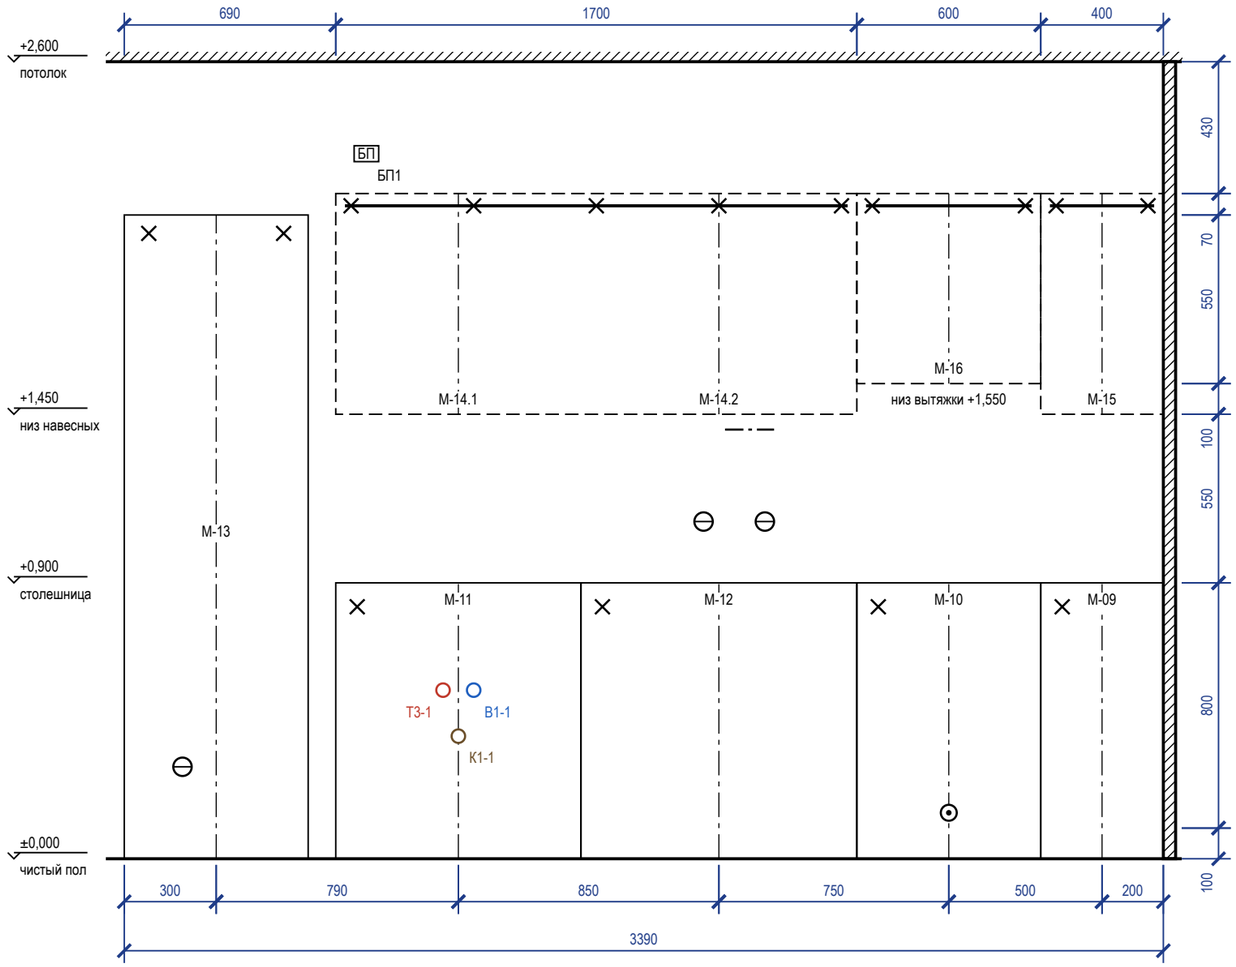

План столешницы (М 1:20)

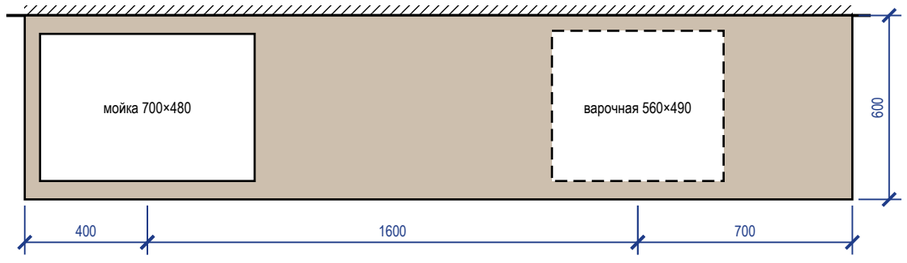

Привязка выводов к осям модулей

Код	Назначение	Модуль	От оси, мм	Н, мм	Размещение
	розетка — холодильник	М-13	−110	300	за пеналом
БП1	блок питания	М-14.1	−300	2300	в навесном модуле
Т3-1	Т3 — межос. 100	М-11	−50	550	в модуле мойки
К1-1	К1 Ø50 — мойка	М-11	0	400	в модуле мойки
В1-1	В1 — межос. 100	М-11	+50	550	в модуле мойки
	розетка — рабочая зона	М-12	−50	1100	над столешницей (фартук)
	светодиодная лента — подсветка столешницы	М-12	+100	1400	в профиле по низу навесного модуля
	розетка ×2 — рабочая зона	М-12	+150	1100	над столешницей (фартук)
	вывод кабеля — варочная панель	М-10	0	150	в соседнем модуле, за ящиком

Зазоры под отделку

Поверхность	Отделка	Зазор, мм	Учесть
фартук	плитка / стеновая панель	10	от чернового основания до корпуса навесных и столешницы
стены	окраска	5	под штукатурку и шпаклёвку за пеналом
пол	инженерная доска		цоколь — после укладки пола, опоры ±20 мм

Условные обозначения


- нижний модуль, пенал (контур)
- невидимый контур: навесной модуль, корпус под столешницей
- ось модуля (от неё — привязка вывода)
- анкер / уголок крепления к стене
- розетка на стене
- вывод кабеля к технике
- B1 — вывод воды В1 / Т3, канализации К1

Примечания


1. Выводы — по проекту электрики и ВК; привязка по горизонтали — от оси модуля (плюс — вправо по виду), по высоте — от чистого пола до оси вывода.
2. Пенал — уголки к стене 2 шт. сверху; нижние модули — стяжками между собой и уголком к стене; ряд выставить по уровню опорами цоколя.
3. Розетки над столешницей — не ниже 150 мм над ней и не за корпусом техники; розетка за ПММ, духовым шкафом и холодильником — только в соседнем модуле или в зоне цоколя с доступом.
4. Столешница — вырезы по шаблонам выбранных моделей мойки и варочной панели; торцы у стены — герметик, пристеночный плинтус.

	Лист	№ док.	Подпись	Дата	Проект: Квартира 65 м²			М 1:20
Дизайнер	Кырлан А.С.			14.11.26	Кухня (пом. 3). Монтажная схема	Стадия	Лист	Листов
Проверил						П	18	105
Н. контр.								
Утв.								

Система хранения М-01 (пом. 1) (М 1:40)

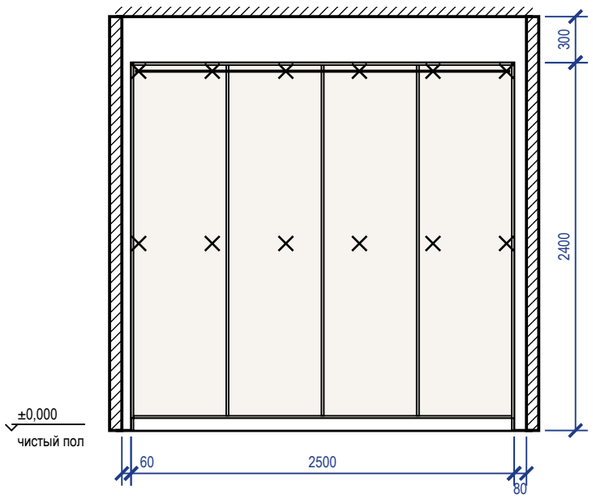


Шкаф-купе М-17 (пом. 4) (М 1:40)

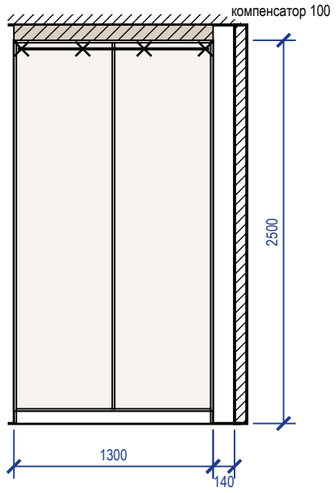


← 700 до стены

Система хранения М-18 (пом. 8) (М 1:40)

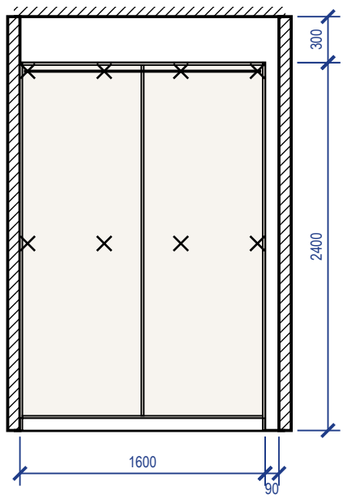

Шкаф распашной М-19 (пом. 9) (М 1:40)

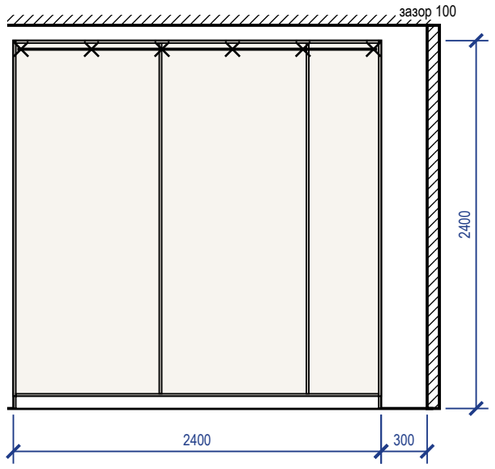

← 2640 до стены

Крепление и зазоры под отделку

Марка	Помещение, стена	Основание	Отделка стены	Зазор, мм	Крепёж по планке	От опрокидывания
М-01	Гардеробная (1), стена А	по основанию — см. таблицу крепежа	окраска	5	анкер 12 шт. (2 ряда)	крепление к стене, 3 точки
М-17	Прихожая (4), стена Б	по основанию — см. таблицу крепежа	окраска	5	анкер 4 шт., шаг 400	уголки 2 шт.
М-18	Кладовая (8), стена Б	по основанию — см. таблицу крепежа	окраска	5	анкер 8 шт. (2 ряда)	уголки 2 шт.
М-19	Детская (9), стена А	по основанию — см. таблицу крепежа	окраска	5	анкер 6 шт., шаг 460	уголки 2 шт.

Крепёж по основанию стены

Основание стены	Крепёж
бетон, ж/б	анкер-шуруп 7,5×72 или дюбель 8×60 с шурупом 5×70
кирпич полнотелый	дюбель 8×80 с шурупом 5×90
газобетон, пазогребень	дюбель для газобетона 10×100 или химический анкер
гипсокартон	закладная до обшивки (брус 40×80 или фанера 18 мм), саморез в закладную

Условные обозначения


- × — анкер / уголок крепления к стене
- корпус и полки ЛДСП (вид на стену)
- компенсатор — короб до потолка

Примечания

1. Установочные размеры — от чистого пола и чистых стен; перед установкой контрольный замер после отделки.
2. Порядок: корпус выставить по уровню опорами цоколя → закрепить к стене по задней планке → навесить двери и фасады, отрегулировать зазоры → подогнать и закрепить компенсатор.
3. Анкеры — с шагом не более 500 мм, не ближе 50 мм от края планки; на ГКЛ только в закладную, установленную до обшивки.
4. Скрытые коммуникации под анкеры проверить детектором; трассы электрики по плану розеток.

	Лист	№ док.	Подпись	Дата	Проект: Квартира 65 м²			М 1:40
Дизайнер	Кырлан А.С.			14.11.26	Шкафы. Монтажная схема	Стадия	Лист	Листов
Проверил						П	19	105
Н. контр.								
Утв.								

выпуск 14.11.2026 № 3aed0ef730 · стр. 19 из 105

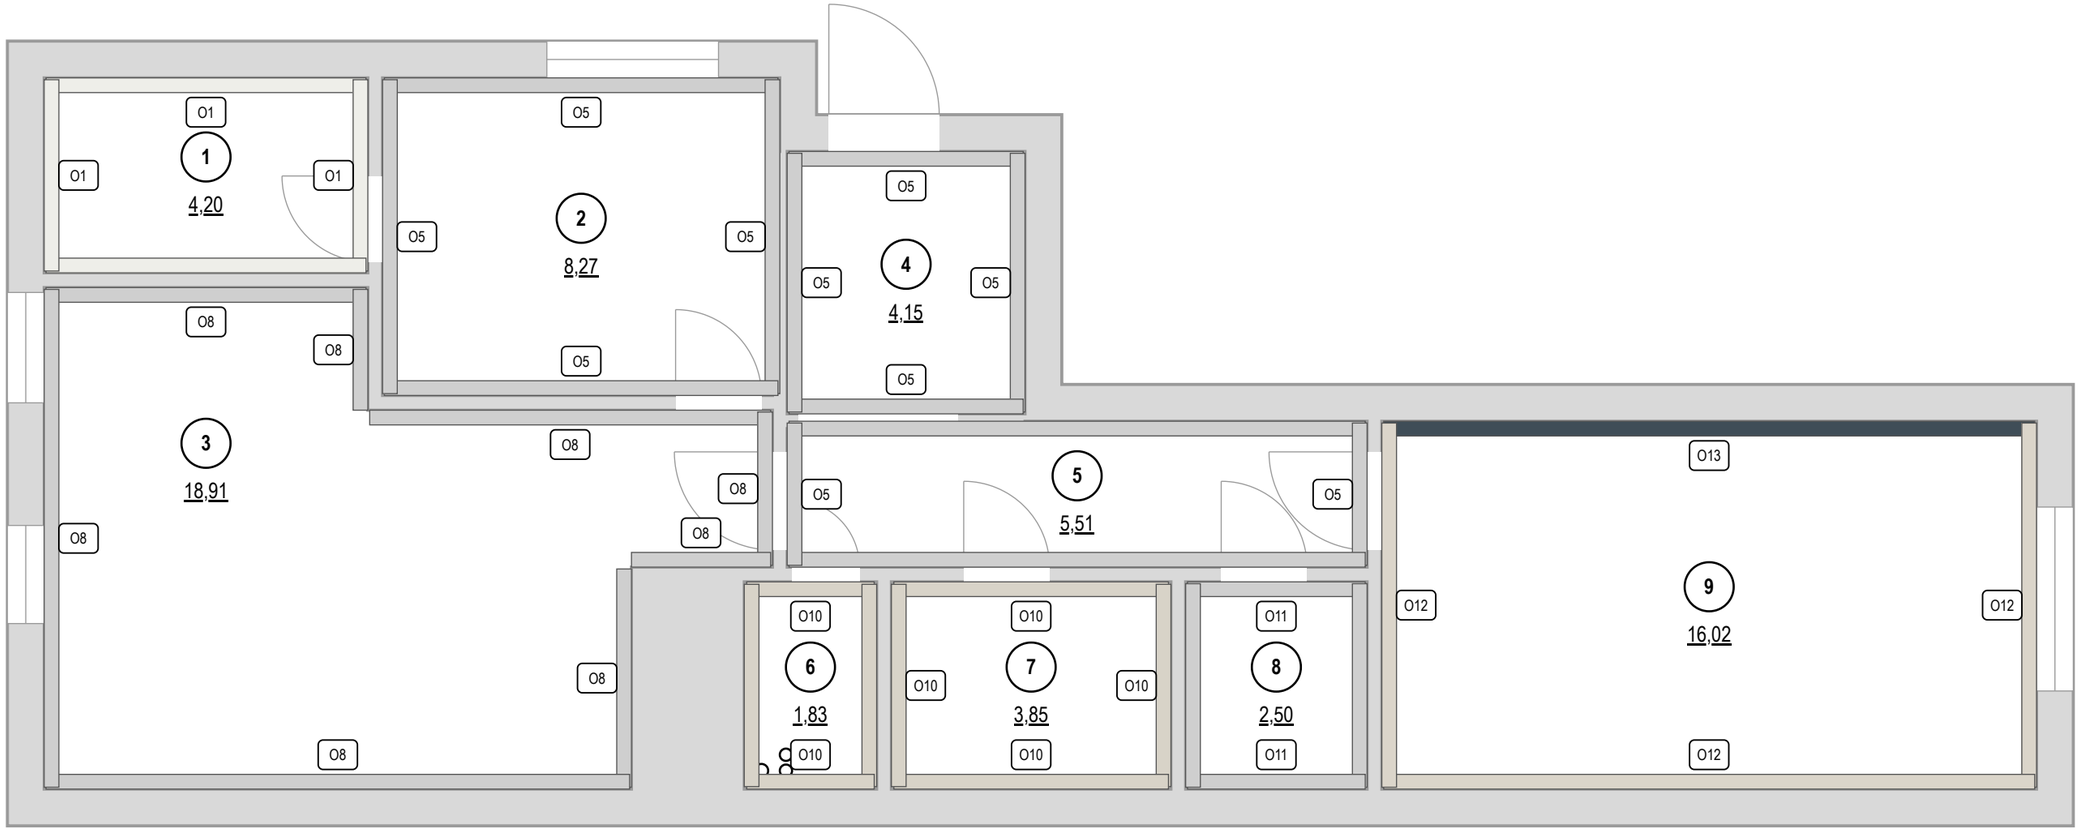

Покрытия стен

Марка	Покрытие	Помещение: S, м²	Итого, м²
O1	окраска Tikkurila · V503 «Winter»	1: 21,0	21,0
O5	окраска Tikkurila · S 1502-Y50R	2: 24,8; 4: 16,3; 5: 20,3	61,4
O8	окраска Tikkurila · S 1002-Y50R	3: 45,7	45,7
O10	облицовка плиткой Italon · 610010001195 «Charme Extra» 600×1200 мм	6: 12,9; 7: 18,9	31,8
O11	окраска Tikkurila · S 0502-Y	8: 15,3	15,3
O12	окраска Farrow & Ball · No. 241 «Skimming Stone»	9: 24,3	24,3
O13	окраска Farrow & Ball · No. 30 «Hague Blue»	9: 13,3	13,3

Площади — нетто, по развёрткам (за вычетом проёмов и фартука); высоты помещений — от чистого пола.

	Лист	№ док.	Подпись	Дата	Проект: Квартира 65 м²			М 1:50
Дизайнер	Кырлан А.С.			14.11.26	Карта покрытий стен	Стадия	Лист	Листов
Проверил						П	20	105
Н. контр.								
Утв.								

выпуск 14.11.2026 № 3aed0ef730 · стр. 20 из 105

Колерная карта по помещениям

Помещение	Поверхность	Образец	Поз.	Система и код цвета	Производитель, линейка / материал, артикул	Блеск	Класс истирания	LRV	Площадь
1. Гардеробная 4,2 м²	стены		**К1**	Tikkurila V503	Tikkurila · Harmony	матовая	1	86	21,4 м²
	потолок		**К2**	Tikkurila V503	Tikkurila · Anti-Reflex 2	глубокомат.	2	86	4,2 м²
	пол		**КМ1**	по образцу	Coswick · Классическая · арт. 1167-1101				4,2 м²
	плинтус		**К3**	Tikkurila V503	Orac Decor · Contour (Luxxus)			86	7,8 м
2. Спальня 8,27 м²	стены		**К4**	NCS S 1502-Y50R	Tikkurila	глубокомат.	2	72	25,1 м²
	потолок		**К5**	NCS S 0300-N	Tikkurila	глубокомат.	2	92	8,3 м²
	пол		**КМ1**	по образцу	Coswick · Классическая · арт. 1167-1101				8,3 м²
	плинтус		**К6**	NCS S 0300-N	Orac Decor · Contour (Luxxus)	полуматов.		92	10,3 м
3. Кухня-гостиная 18,91 м²	стены		**К7**	NCS S 1002-Y50R	Tikkurila	полуматов.	1	82	46,3 м²
	потолок		**К8**	NCS S 0300-N	Tikkurila	глубокомат.	1	92	18,9 м²
	пол		**КМ1**	по образцу	Coswick · Классическая · арт. 1167-1101				18,9 м²
	плинтус		**К6**	NCS S 0300-N	Orac Decor · Contour (Luxxus)	полуматов.		92	18,6 м
4. Прихожая 4,15 м²	стены		**К9**	NCS S 1502-Y50R	Tikkurila	полуматов.	1	72	16,6 м²
	потолок		**К8**	NCS S 0300-N	Tikkurila	глубокомат.	1	92	4,2 м²
	пол		**КМ2**	Королевская дорога	Kerama Marazzi · арт. SG501600R				4,2 м²
	плинтус		**К6**	NCS S 0300-N	Orac Decor · Contour (Luxxus)	полуматов.		92	6,0 м
5. Коридор 5,51 м²	стены		**К9**	NCS S 1502-Y50R	Tikkurila	полуматов.	1	72	20,6 м²
	потолок		**К8**	NCS S 0300-N	Tikkurila	глубокомат.	1	92	5,5 м²
	пол		**КМ2**	Королевская дорога	Kerama Marazzi · арт. SG501600R				5,5 м²
	плинтус		**К6**	NCS S 0300-N	Orac Decor · Contour (Luxxus)	полуматов.		92	7,0 м
6. Санузел 1,83 м²	стены		**КМ3**	Charme Extra	Italon · арт. 610010001195				13,3 м²
	потолок		**К8**	NCS S 0300-N	Tikkurila	глубокомат.	1	92	1,8 м²
	пол		**КМ2**	Королевская дорога	Kerama Marazzi · арт. SG501600R				1,8 м²
7. Ванная 3,85 м²	стены		**КМ3**	Charme Extra	Italon · арт. 610010001195				19,3 м²
	потолок		**К8**	NCS S 0300-N	Tikkurila	глубокомат.	1	92	3,9 м²
	пол		**КМ2**	Королевская дорога	Kerama Marazzi · арт. SG501600R				3,9 м²
8. Кладовая 2,5 м²	стены		**К10**	NCS S 0502-Y	Tikkurila	матовая	2	86	15,6 м²
	потолок		**К5**	NCS S 0300-N	Tikkurila	глубокомат.	2	92	2,5 м²
	пол		**КМ1**	по образцу	Coswick · Классическая · арт. 1167-1101				2,5 м²
	плинтус		**К6**	NCS S 0300-N	Orac Decor · Contour (Luxxus)	полуматов.		92	5,6 м
9. Детская 16,02 м²	стены		**К11**	Farrow & Ball No. 241	Farrow & Ball · Modern Emulsion	матовая	1	67	24,3 м²
	акцент А		**К12**	Farrow & Ball No. 30	Farrow & Ball · Modern Emulsion	матовая	1	7	13,3 м²
	потолок		**К2**	Tikkurila V503	Tikkurila · Anti-Reflex 2	глубокомат.	2	86	16,0 м²
	пол		**КМ1**	по образцу	Coswick · Классическая · арт. 1167-1101				16,0 м²
	плинтус		**К13**	Farrow & Ball No. 241	Orac Decor · Contour (Luxxus)			67	15,9 м

Примечания

1. Цвет на листе и на экране — ориентир. До покраски — выкрас на объекте: не меньше А3 (или лист ГКЛ), на грунте под эту краску, не на белой шпаклёвке, в 2 слоя; на обороте — код, бренд, веер, дата. Смотреть днём и вечером, рядом с образцами пола и плитки; к основному цвету стен — ещё 2 соседних оттенка. Красить только в цвет утверждённого выкраса.
2. Краску заказывать по коду из графы «Система и код цвета» у бренда этого кода, не «аналогом» другого; весь объём одного кода — одной партией, колеруемую краску — за один проход машины.
3. Площади — те же, что в ведомости отделки (лист С1); сколько краски заказать — в спецификации отделочных материалов (лист С2).

Схема палитры проекта

Стиль: Скандинавский · схема: нейтральная

основной	основной	основной	основной	второстепенный	второстепенный	акцентный
NCS S 1502-Y50R	**NCS S 1002-Y50R**	**NCS S 0300-N**	**Tikkurila V503**	**Farrow & Ball No. 241**	**NCS S 0502-Y**	**Farrow & Ball No. 30**
тёплый светло-серый LRV 72 стены 2,4,5	тёплый светлый грейж LRV 82 стены 3	белый LRV 92 потолок 2,3,4,5,6,7,8; плинтус 2,3,4,5,8	Winter LRV 86 стены 1; потолок 1,9; плинтус 1; текстиль/декор 9	Skimming Stone LRV 67 стены 9; плинтус 9; текстиль/декор 4,7	белый сёдзи/сиккуй — известь, васи LRV 86 стены 8	Hague Blue LRV 7 акцент 9; текстиль/декор 9

План 60/30/10

60%	30%	10%

Окраска, факт — по площади стен, акцентов, потолков

79%	16%	

окрашено всего 248,5 м²; второстепенный тон несут мебель и текстиль

Текстиль и декор в цветах вне палитры проекта

- Tikkurila G503 Calla — пом. 2 (Т6, Т15), 3 (Т1, Т2, Т3), 7 (Т19)
- NCS S 2002-Y серый камень, тёплый — пом. 2 (Т13)
- Farrow & Ball No. 231 Setting Plaster — пом. 2 (Т14)
- Farrow & Ball No. 299 De Nimes — пом. 2 (Т16), 3 (Т4), 7 (Т18)
- NCS S 3020-Y80R приглушённая терракота/пудра — пом. 3 (Т5)
- Tikkurila H487 Pumice — пом. 9 (Т7)
- Tikkurila V484 Driftwood — пом. 9 (Т9)
- Farrow & Ball No. 229 Elephant's Breath — пом. 9 (Т10)
- Farrow & Ball No. 47 Green Smoke — пом. 9 (Т11)

Условные обозначения

- **К1** Tikkurila V503 · Winter · Harmony · матовая · кл. 1
- **К2** Tikkurila V503 · Winter · Anti-Reflex 2 · глубокомат. · кл. 2
- **К3** Tikkurila V503 · Winter · Contour (Luxxus)
- **К4** NCS S 1502-Y50R · Tikkurila · глубокомат. · кл. 2
- **К5** NCS S 0300-N · Tikkurila · глубокомат. · кл. 2
- **К6** NCS S 0300-N · Orac Decor Contour (Luxxus) · полуматов.
- **К7** NCS S 1002-Y50R · Tikkurila · полуматов. · кл. 1
- **К8** NCS S 0300-N · Tikkurila · глубокомат. · кл. 1
- **К9** NCS S 1502-Y50R · Tikkurila · полуматов. · кл. 1
- **К10** NCS S 0502-Y · Tikkurila · матовая · кл. 2
- **К11** Farrow & Ball No. 241 · Skimming Stone · Modern Emulsion · матовая · кл. 1
- **К12** Farrow & Ball No. 30 · Hague Blue · Modern Emulsion · матовая · кл. 1
- **К13** Farrow & Ball No. 241 · Skimming Stone · Contour (Luxxus)
- **КМ1** инженерная доска · 1167-1101
- **КМ2** керамогранит · SG501600R
- **КМ3** плитка · 610010001195

дерево (доска, паркет, ламинат) — рисунок досок

керамогранит, плитка, камень — сетка швов по формату

плашка не залита — цвет только по коду и вееру бренда

К — краска, КМ — отделочный материал (тон КМ — по описанию, эталон — образец материала); кл. — класс истирания (1 — самый стойкий к мытью); LRV — светлота цвета: 0 — чёрный, 100 — белый

Перечень выкрасов на согласование

№	Код	Бренд / веер	Пом. / стена	Подложка	Формат	Статус

… ещё 7 выкрасов — в ведомости отделки

	Лист	№ док.	Подпись	Дата	Проект: Квартира 65 м²			
Дизайнер	Кырлан А.С.			14.11.26				
Проверил					Колерная карта	Стадия	Лист	Листов
Н. контр.						П	21	105
Утв.								


выпуск 14.11.2026 № 3aed0ef730 · стр. 21 из 105

Экспликация помещений

лист 16 · на плане — номера в марках

Ведомость мебели и оборудования

25 позиц. (27 шт.) — расшифровка марок:
полностью на листе 23 «Спецификация мебели и оборудования»
марка, наименование, Ш×Г×В, материал, модель,
допуск замены. Марки на плане — по ней.

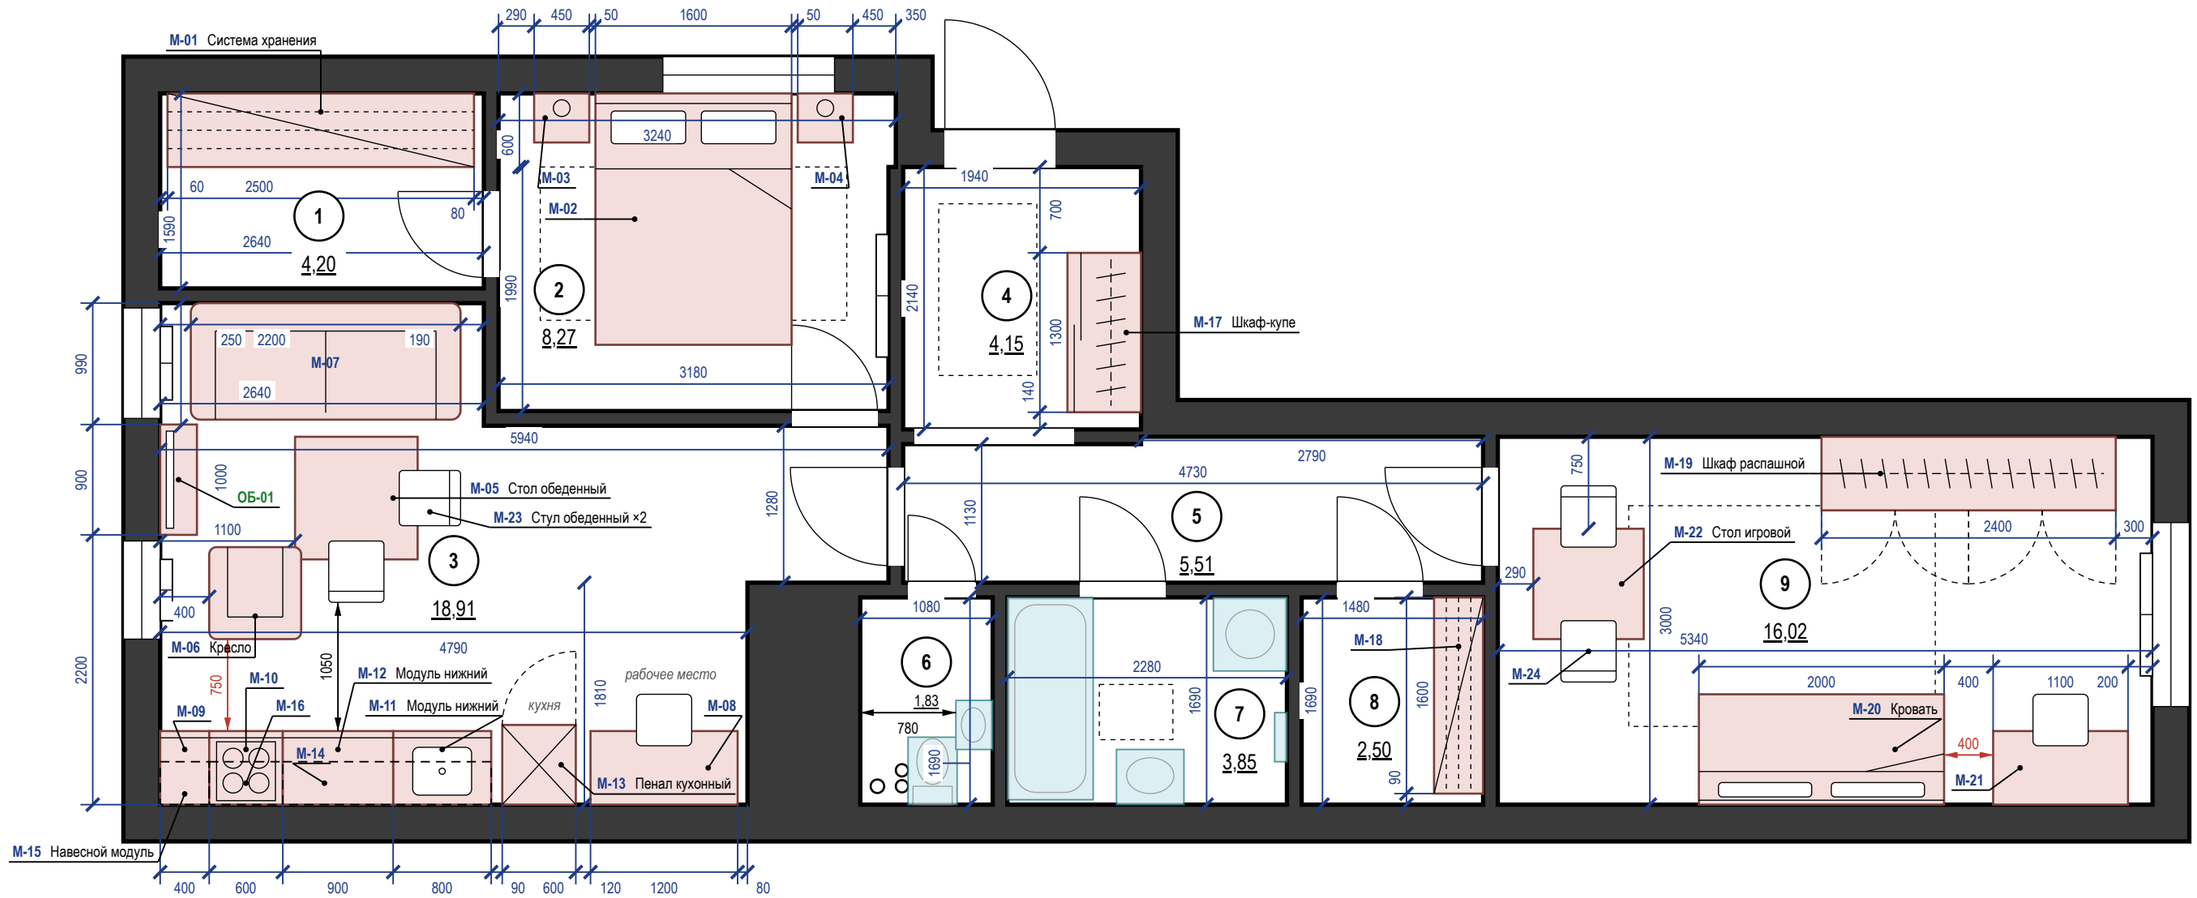

Примечания

1. Размеры — в мм от чистовых поверхностей стен; габариты предметов (Ш×Г×В) — в ведомости мебели, лист 23, на плане марка и короткое имя; размеры мебели уточнить после отделочных работ; общие указания — лист 14.
2. У позиций М-02, М-03, М-04, ОБ-01, М-07, М-08, М-09, М-10, М-14, М-16, М-18, М-21, М-24 на плане только марка: наименование и габарит — в спецификации, лист 23.
3. Стулья обеденной группы (М-23 — 2 шт., М-24 — 2 шт.) показаны в рабочем положении, задвинутыми под столешницу на 150 мм.

	Лист	№ док.	Подпись	Дата	Проект: Квартира 65 м²	М 1:50		
Дизайнер	Кырлан А.С.			14.11.26	План размещения мебели и оборудования	Стадия	Лист	Листов
Проверил						П	22	105
Н. контр.								
Утв.								

выпуск 14.11.2026 № 3aed0ef730 · стр. 22 из 105

Поз.	Наименование и техническая характеристика	Тип, марка, обозначение документа, опросного листа	Код продукции	Поставщик	Ед. измерения	Кол.	Масса 1 ед., кг	Примечание
	Мебель встроенная и корпусная (изготовление по чертежам мебельщика)							
М-01	Система хранения: штанги, полки, ящики; каркас и полки — ЛДСП 16 мм, декор «дуб натуральный»; без фасадов; Ш×Г×В 2500×600×2400 мм	—	—	изготовление на заказ	шт.	1	—	пом. 1; крепление к стене
М-09	Модуль нижний; корпус ЛДСП 16 мм; фасады — МДФ эмаль 18 мм; Ш×Г×В 400×600×900 мм	—	—	изготовление на заказ	шт.	1	—	пом. 3
М-10	Модуль нижний, варочная; корпус ЛДСП 16 мм; фасады — МДФ эмаль 18 мм; Ш×Г×В 600×600×900 мм	—	—	изготовление на заказ	шт.	1	—	пом. 3
М-11	Модуль нижний, мойка; корпус ЛДСП 16 мм; фасады — МДФ эмаль 18 мм; Ш×Г×В 800×600×900 мм	—	—	изготовление на заказ	шт.	1	—	пом. 3
М-12	Модуль нижний; корпус ЛДСП 16 мм; фасады — МДФ эмаль 18 мм; Ш×Г×В 900×600×900 мм	—	—	изготовление на заказ	шт.	1	—	пом. 3
М-13	Пенал кухонный, холодильник; корпус ЛДСП 16 мм; фасады — без фасада (прибор отдельностоящий); Ш×Г×В 600×650×2100 мм	—	—	изготовление на заказ	шт.	1	—	пом. 3
М-14	Модуль навесной; корпус ЛДСП 16 мм; фасады — МДФ эмаль 18 мм; Ш×Г×В 1700×350×720 мм	—	—	изготовление на заказ	шт.	1	—	пом. 3
М-15	Навесной модуль; корпус ЛДСП 16 мм; фасады — МДФ эмаль 18 мм; Ш×Г×В 400×350×720 мм	—	—	изготовление на заказ	шт.	1	—	пом. 3
М-16	Навесной модуль над варочной, вытяжка встраивается в дно; корпус ЛДСП 16 мм; фасады — МДФ эмаль 18 мм; Ш×Г×В 600×350×620 мм	—	—	изготовление на заказ	шт.	1	—	пом. 3
М-17	Шкаф-купе; корпус ЛДСП 16 мм; фасады — ЛДСП 10 мм в алюминиевом профиле; Ш×Г×В 1300×600×2500 мм	—	—	изготовление на заказ	шт.	1	—	пом. 4
М-18	Стеллаж кладовой; каркас и полки — ЛДСП 16 мм, декор «дуб натуральный»; без фасадов; Ш×Г×В 1600×400×2400 мм	—	—	изготовление на заказ	шт.	1	—	пом. 8
М-19	Шкаф распашной; корпус ЛДСП 16 мм; фасады — МДФ 18 мм, эмаль матовая; цвет фасадов — в цвет стен (Farrow & Ball No. 241); Ш×Г×В 2400×600×2400 мм	—	—	изготовление на заказ	шт.	1	—	пом. 9
	Мебель покупная							
М-02	Кровать двуспальная; мягкое изголовье, обивка — ткань, цвет Farrow & Ball No. 241; Ш×Г×В 1600×2050×450 мм	аналог: Ш×Г×В 1600×2050×450 мм, мягкое изголовье	—	аналог по характеристикам	шт.	1	—	пом. 2; замена ≤ габарита
М-03, М-04	Тумба прикроватная; шпон, дуб натуральный, матовое масло; Ш×Г×В 450×400×500 мм	аналог: Ш×Г×В 450×400×500 мм, шпон	—	аналог по характеристикам	шт.	2	—	пом. 2; замена ≤ габарита
М-05	Стол обеденный круглый Ø1000; шпон, дуб натуральный, матовое масло; Ш×Г×В 1000×1000×750 мм	аналог: Ш×Г×В 1000×1000×750 мм, шпон	—	аналог по характеристикам	шт.	1	—	пом. 3; замена ≤ габарита
М-06	Кресло; обивка — ткань, цвет Farrow & Ball No. 241; Ш×Г×В 750×750×800 мм	аналог: Ш×Г×В 750×750×800 мм, обивка — ткань	—	аналог по характеристикам	шт.	1	—	пом. 3; замена ≤ габарита
М-07	Диван; обивка — ткань, цвет Farrow & Ball No. 241; Ш×Г×В 2200×950×850 мм	аналог: Ш×Г×В 2200×950×850 мм, обивка — ткань	—	аналог по характеристикам	шт.	1	—	пом. 3; замена ≤ габарита
М-08	Стол рабочий (кабинет); шпон, дуб натуральный, матовое масло; Ш×Г×В 1200×600×750 мм	аналог: Ш×Г×В 1200×600×750 мм, шпон	—	аналог по характеристикам	шт.	1	—	пом. 3; замена ≤ габарита
М-23	Стул обеденный к столу М-05; обивка — ткань, цвет Farrow & Ball No. 241; каркас — дуб натуральный; Ш×Г×В 450×500×820 мм	аналог: Ш×Г×В 450×500×820 мм, обивка — ткань	—	аналог по характеристикам	шт.	2	—	пом. 3; замена ≤ габарита
ОБ-01	ТВ на стене, тумба подвесная; шпон, дуб натуральный, матовое масло; Ш×Г×В 900×300×450 мм	аналог: Ш×Г×В 900×300×450 мм, шпон	—	аналог по характеристикам	шт.	1	—	пом. 3; замена ≤ габарита
М-20	Кровать односпальная 900×2000; мягкое изголовье, обивка — ткань, цвет Farrow & Ball No. 241; Ш×Г×В 2000×900×450 мм	аналог: Ш×Г×В 2000×900×450 мм, мягкое изголовье	—	аналог по характеристикам	шт.	1	—	пом. 9; замена ≤ габарита
М-21	Стол письменный; шпон, дуб натуральный, матовое масло; Ш×Г×В 1100×600×750 мм	аналог: Ш×Г×В 1100×600×750 мм, шпон	—	аналог по характеристикам	шт.	1	—	пом. 9; замена ≤ габарита
М-22	Стол игровой круглый Ø900; шпон, дуб натуральный, матовое масло; Ш×Г×В 900×900×600 мм	аналог: Ш×Г×В 900×900×600 мм, шпон	—	аналог по характеристикам	шт.	1	—	пом. 9; замена ≤ габарита
М-24	Стул обеденный к столу М-22; обивка — ткань, цвет Farrow & Ball No. 241; каркас — дуб натуральный; Ш×Г×В 450×500×820 мм	аналог: Ш×Г×В 450×500×820 мм, обивка — ткань	—	аналог по характеристикам	шт.	2	—	пом. 9; замена ≤ габарита

Примечания

1. Позиции мебели совпадают с марками на плане расстановки; размеры Ш×Г×В — Ш вдоль стены, Г от стены.
2. Размеры и привязки плана расстановки — в мм от чистовых поверхностей стен: слой штукатурки 20 мм по блоку и 5 мм шпаклёвки по ГКЛ учтён; привязки — от стен и углов помещения, а не от другой мебели.
3. План расстановки не является документацией для изготовления мебели. Встроенная и корпусная мебель изготавливается по чертежам мебельщика после контрольного обмера (после штукатурки); «стена в стену» — с зазором 10 мм с каждой стороны или с компенсаторами; графы «Тип, марка» и «Код продукции» для неё не заполняются (ГОСТ 21.110-2013).
4. Покупные изделия — аналог по характеристикам: заменять только на изделия не больше указанного габарита и того же материала и цвета.
5. Материал и цвет, не указанные в данных изделия, приняты по концепции: тон дерева — по полу, обивка — по вторичному цвету палитры; образцы согласовать до заказа.
6. Масса 1 ед. для изделий до 25 кг не указывается. Техника — по монтажным схемам изготовителя; выводы — по листам ЭОМ и ВК.

	Лист	№ док.	Подпись	Дата
Дизайнер	Кырлан А.С.			14.11.26
Проверил				
Н. контр.				
Утв.				

Проект: Квартира 65 м²

Спецификация мебели и оборудования	Стадия	Лист	Листов
	П	23	105

выпуск 14.11.2026 № 3aed0ef730 · стр. 23 из 105

Поз.	Наименование и техническая характеристика	Тип, марка, обозначение документа, опросного листа	Код продукции	Поставщик	Ед. измерения	Кол.	Масса 1 ед., кг	Примечание
	Техника встраиваемая и бытовая (покупные изделия), светильники под розетки							
	Холодильник, в модуле М-13	аналог по характеристикам: отдельностоящий, габарит — по проёму	—	по выбору заказчика до изготовления мебели	шт.	1	—	пом. 3; по схеме изготовителя
	Варочная панель встраиваемая, индукционная, в модуле М-10	аналог по характеристикам: индукционная 60 см, вырез 560 × 490 мм по шаблону модели	—	по выбору заказчика до изготовления мебели	шт.	1	—	пом. 3; по схеме изготовителя
	Вытяжка встраиваемая, в модуле М-16	аналог по характеристикам: производительность — по расчёту ОВ, шум ≤ 55 дБ(А)	—	по выбору заказчика до изготовления мебели	шт.	1	—	пом. 3; по схеме изготовителя
	Стиральная машина, место по листу ВК (ОБ-02); Ш×Г 600×600 мм	аналог по характеристикам: тип загрузки — по листу ВК, в плане 600 × 600 мм (ширина × глубина), по листу ВК	—	по выбору заказчика до изготовления мебели	шт.	1	—	пом. 7; по схеме изготовителя
	Торшер, у поз. М-06; абажур — ткань или опаловое стекло; лампа 3000 K	—	—	аналог по характеристикам	шт.	1	—	пом. 3; розетка — по плану розеток (ЭОМ)
	Торшер, у поз. М-20; абажур — ткань или опаловое стекло; лампа 2700 K	—	—	аналог по характеристикам	шт.	1	—	пом. 9; розетка Р11 (ЭОМ)
	Текстиль							
Т6	Римская штора льняная с блэкаут-подкладкой, молочная; лён 100 %; цвет Tikkurila G503; карниз 1500 мм, высота 1750 мм	—	—	аналог по характеристикам	шт.	1	—	пом. 2
Т13	Ковёр шерстяной 2500×1250 под кроватью, выходит по бокам на 450 мм, овсяный; шерсть 100 %; цвет NCS S 2002-Y; 2500×1250 мм	—	—	аналог по характеристикам	шт.	1	—	пом. 2; с подложкой
Т14	Подушки декоративные на кровать, лён, пыльно-розовый; лён 100 %; цвет Farrow & Ball No. 231	—	—	аналог по характеристикам	шт.	2	—	пом. 2
Т15	Подушка-валик на кровать, букле молочное; букле (шерсть 60 %, полиэстер 40 %); цвет Tikkurila G503	—	—	аналог по характеристикам	шт.	1	—	пом. 2
Т16	Плед шерстяной в изножье кровати, приглушённый синий; шерсть мериноса 100 %; цвет Farrow & Ball No. 299	—	—	аналог по характеристикам	шт.	1	—	пом. 2
Т1	Римская штора льняная, молочная (окно 1); лён 100 %; цвет Tikkurila G503; карниз 1000 мм, высота 1750 мм	—	—	аналог по характеристикам	шт.	1	—	пом. 3
Т2	Римская штора льняная, молочная (окно 2); лён 100 %; цвет Tikkurila G503; карниз 900 мм, высота 1750 мм	—	—	аналог по характеристикам	шт.	1	—	пом. 3
Т3	Подушки на диван, букле молочное; букле (шерсть 60 %, полиэстер 40 %); цвет Tikkurila G503	—	—	аналог по характеристикам	шт.	3	—	пом. 3
Т4	Подушки на диван, лён, приглушённый синий; лён 100 %; цвет Farrow & Ball No. 299	—	—	аналог по характеристикам	шт.	2	—	пом. 3
Т5	Плед шерстяной на диван, терракота; шерсть мериноса 100 %; цвет NCS S 3020-Y80R	—	—	аналог по характеристикам	шт.	1	—	пом. 3
Т17	Ковёр — дорожка-коврик хлопковая тканая 800×1400, светлая; хлопок 100 %; цвет Farrow & Ball No. 241; 800×1400 мм	—	—	аналог по характеристикам	шт.	1	—	пом. 4; с подложкой
Т18	Полотенца банные махровые, приглушённый синий, сложены на полотенцесушителе; хлопок 100 %; цвет Farrow & Ball No. 299	—	—	аналог по характеристикам	шт.	2	—	пом. 7
Т19	Полотенца для рук вафельные, молочные, на нижних перекладинах сушителя; хлопок 100 %; цвет Tikkurila G503	—	—	аналог по характеристикам	шт.	2	—	пом. 7
Т20	Ковёр — коврик для ванной у бортика ванны, хлопок тафтинг, светлый каменный; хлопок 100 %, латексная противоскользящая основа; цвет Farrow & Ball No. 241; 600×450 мм	—	—	аналог по характеристикам	шт.	1	—	пом. 7; с подложкой
Т7	Портьеры-волна; лён 100 %; цвет Tikkurila H487; карниз 1820 мм, высота 2590 мм, сборка 2	—	—	аналог по характеристикам	шт.	2	—	пом. 9
Т8	Тюль; полиэстер 100 %; цвет Tikkurila V503; карниз 1820 мм, высота 2590 мм, сборка 2,5	—	—	аналог по характеристикам	шт.	1	—	пом. 9

	Лист	№ док.	Подпись	Дата
Дизайнер	Кырлан А.С.			14.11.26
Проверил				
Н. контр.				
Утв.				

Проект: Квартира 65 м²

Спецификация мебели и оборудования (продолжение)

Стадия	Лист	Листов
П	24	105

выпуск 14.11.2026 № 3aed0ef730 · стр. 24 из 105

Поз.	Наименование и техническая характеристика	Тип, марка, обозначение документа, опросного листа	Код продукции	Поставщик	Ед. измерения	Кол.	Масса 1 ед., кг	Примечание
Т9	Ковёр под кроватью; шерсть 100 %; цвет Tikkurila V484; 2500×1800 мм	—	—	аналог по характеристикам	шт.	1	—	пом. 9; с подложкой
Т10	Подушки декоративные на кровать; букле (шерсть 60 %, полиэстер 40 %); цвет Farrow & Ball No. 229	—	—	аналог по характеристикам	шт.	3	—	пом. 9
Т11	Подушки на кровать, акцент; хлопковый бархат 100 %; цвет Farrow & Ball No. 47	—	—	аналог по характеристикам	шт.	2	—	пом. 9
Т12	Плед на кровать; шерсть мериноса 100 %; цвет Farrow & Ball No. 30	—	—	аналог по характеристикам	шт.	1	—	пом. 9
	Декор							
ДК6	Картина напротив кровати: акварель в паспарту, дубовая рама 1000×700; 1000×700 мм; центр на 1500 мм от пола	—	—	аналог по характеристикам	шт.	1	4	пом. 2; крепление: дюбель с крюком, 2 точки
ДК7	Зеркало в рост в тонкой дубовой раме 500×1600; 500×1600 мм; низ на 300 мм от пола	—	—	аналог по характеристикам	шт.	1	12	пом. 2; крепление: анкер для пустотелых оснований, 4 шт.
ДК1	Картина над диваном: абстракция, холст в тонкой дубовой раме 1400×900; 1400×900 мм; низ на 1050 мм от пола	—	—	аналог по характеристикам	шт.	1	6	пом. 3; крепление: анкер, 2 шт.
ДК2	Сансевиерия в напольном керамическом кашпо Ø300, матовый белый; 350×350 мм	—	—	аналог по характеристикам	шт.	1	—	пом. 3
ДК5	Ваза керамическая матовая с сухой веткой на обеденном столе, молочная; 200×300 мм; на М-05	—	—	аналог по характеристикам	шт.	1	—	пом. 3
ДК8	Зеркало в рост в дубовой раме 500×1600; 500×1600 мм; низ на 300 мм от пола	—	—	аналог по характеристикам	шт.	1	12	пом. 4; крепление: анкер для пустотелых оснований, 4 шт.
ДК9	Постер в дубовой раме 400×560, левый (группа «триптих»): графика тушью; 400×560 мм; центр на 1500 мм от пола	—	—	аналог по характеристикам	шт.	1	2	пом. 5; крепление: дюбель с крюком, 2 точки
ДК10	Постер в дубовой раме 400×560, средний (группа «триптих»): графика тушью; 400×560 мм; центр на 1500 мм от пола	—	—	аналог по характеристикам	шт.	1	2	пом. 5; крепление: дюбель с крюком, 2 точки
ДК11	Постер в дубовой раме 400×560, правый (группа «триптих»): графика тушью; 400×560 мм; центр на 1500 мм от пола	—	—	аналог по характеристикам	шт.	1	2	пом. 5; крепление: дюбель с крюком, 2 точки
ДК12	Зеркало над умывальником, влагостойкое, в тонкой дубовой раме 400×600; 400×600 мм; низ на 1150 мм от пола	—	—	аналог по характеристикам	шт.	1	5	пом. 6; крепление: клей для зеркал + 2 опорных уголка снизу
ДК14	Постер в тонкой дубовой раме 300×400: чайка над водой, линейный рисунок; 300×400 мм; низ на 1300 мм от пола	—	—	аналог по характеристикам	шт.	1	1	пом. 6; крепление: дюбель с крюком, 1 точка
ДК13	Зеркало над умывальником, влагостойкое, в тонкой дубовой раме 550×650; 550×650 мм; низ на 1150 мм от пола	—	—	аналог по характеристикам	шт.	1	5	пом. 7; крепление: клей для зеркал + 2 опорных уголка снизу
ДК3	Картина над кроватью: графика в паспарту, рама — дуб; 1000×700 мм; низ на 1300 мм от пола	—	—	аналог по характеристикам	шт.	1	4	пом. 9; крепление к стене
ДК4	Зеркало в рост в тонкой чёрной раме; рама — чёрный матовый; 600×1600 мм; низ на 300 мм от пола	—	—	аналог по характеристикам	шт.	1	12	пом. 9; крепление: анкер для пустотелых оснований, 4 шт.

	Лист	№ док.	Подпись	Дата
Дизайнер	Кырлан А.С.			14.11.26
Проверил				
Н. контр.				
Утв.				

Проект: Квартира 65 м²

Спецификация мебели и оборудования (продолжение)

Стадия	Лист	Листов
П	25	105

Ведомость изделий

Марка	Наименование	Пом.	Ш×Г×В, мм	Корпус	Фасад	Кромка, мм	Кол.
М-01	Система хранения	1	2500×600×2400	ЛДСП 16	без фасадов	0,4 / 2 *	1
М-17	Шкаф-купе	4	1300×600×2500	ЛДСП 16	ЛДСП 10 мм в алюминиевом профиле	0,4 / 1	1
М-18	Система хранения	8	1600×400×2400	ЛДСП 16	без фасадов	0,4 / 2 *	1
М-19	Шкаф распашной	9	2400×600×2400	ЛДСП 16	МДФ 18 мм, эмаль матовая	0,4 / 2 *	1
М-13	Место под холодильник отдельностоящий: без корпуса и фасада	3	600×650×2100 (место в ряду)	без корпуса	без фасада (прибор отдельностоящий)		
М-11	Модуль нижний: мойка	3	800×600×900	ЛДСП 16	МДФ эмаль 18 мм	0,4 / 1	1
М-14	Модуль навесной: сушка, полки	3	1700×350×720	ЛДСП 16	МДФ эмаль 18 мм	0,4 / 1	1
М-12	Модуль нижний: ящики	3	900×600×900	ЛДСП 16	МДФ эмаль 18 мм	0,4 / 1	1
М-10	Модуль нижний: ящики, варочная	3	600×600×900	ЛДСП 16	МДФ эмаль 18 мм	0,4 / 1	1
М-16	Модуль навесной: полки	3	600×350×620	ЛДСП 16	МДФ эмаль 18 мм	0,4 / 1	1
М-09	Модуль нижний: ящики	3	400×600×900	ЛДСП 16	МДФ эмаль 18 мм	0,4 / 1	1
М-15	Модуль навесной: полки	3	400×350×720	ЛДСП 16	МДФ эмаль 18 мм	0,4 / 1	1

Ведомость встраиваемой техники

Поз.	Прибор	Ниша, вырез, мм	Вентиляция	Питание	Схема
М-13	Холодильник отдельностоящий	проём 600, зазор сверху ≥ 50	по паспорту модели	М-13, H=300 — за пеналом	по модели
М-11	Мойка врезная / подстольная с сифоном	вырез по шаблону, ориентир 700 × 480		смеситель — выводы ВК	по модели
М-10	Варочная панель индукционная, 60 см	вырез в столешнице 560 × 490		М-10, H=150 — в соседнем модуле, за ящиком	по модели
М-16	Вытяжка встраиваемая в навесной модуль, 60 см	низ ≥ 650 над панелью	воздуховод к вентканалу, короб до потолка	питание: точка ЭОМ не задана — вывод под прибор не делать до задания	по модели

Ведомость фурнитуры


№	Фурнитура	Тип, размер	Изделия	Кол.
1	Полкодержатель с фиксацией	ø5 мм	М-01, М-17, М-18, М-19, М-14, М-16, М-15	140
2	Штанга овальная 30×15, L = 605	+ 2 держателя	М-01	2
3	Опора регулируемая с цоколем на клипсах	ход 20 мм	М-01, М-17, М-18, М-19	30
4	Анкер по основанию стены	по таблице крепежа	М-01, М-17, М-18, М-19, М-14, М-16, М-15	39
5	Уголок крепления к стене от опрокидывания	стальной	М-01, М-17, М-18, М-19	8
6	Система дверей купе: профиль, направляющие, ролики	на 2 двери	М-17	1
7	Ручка-профиль вертикальная	в цвет профиля	М-17	2
8	Штанга овальная 30×15, L = 626	+ 2 держателя	М-17	1
9	Полка для обуви выдвижная наклонная	ширина 626	М-17	3
10	Штанга выдвижная торцевая	L по глубине	М-18	1
11	Петля накладная 110° с доводчиком	чашка 35 мм	М-19, М-11, М-14, М-16, М-15	48
12	Штанга овальная 30×15, L = 936	+ 2 держателя	М-19	2
13	Штанга овальная 30×15, L = 456	+ 2 держателя	М-19	1
14	Ручка-профиль	латунь матовая	М-11, М-14, М-12, М-10, М-16, М-09, М-15	18
15	Опора кухонная регулируемая 100–120 мм	+ клипса цоколя	М-11, М-12, М-10, М-09	20
16	Сушка для посуды в шкаф	ширина 800	М-14	1
17	Навес регулируемый для навесного шкафа	пара на секцию	М-14, М-16, М-15	4
18	Шина монтажная	L = 1640	М-14	1
19	Направляющие полного выдвижения с доводчиком NL 500	пара	М-12, М-10, М-09	9
20	Шина монтажная	L = 540	М-16	1
21	Шина монтажная	L = 340	М-15	1

Примечания


1. Модели техники выбирает заказчик до изготовления мебели; ниши, вырезы и вентиляция — по монтажной схеме выбранной модели (условие гарантии), её номер вносится в ведомость.
2. Количество фурнитуры — по чертежам изделий; запас крепежа 5 %. Аналоги — по характеристикам (доводчик, нагрузка, ход).
3. Цвет корпусов, фасадов и профилей — по колерной карте проекта. Кромка — скрытые / видимые торцы, мм.
4. Кромка в данных изделия не задана: принята ПВХ 0,4 мм на скрытых торцах и 2 мм на видимых (по умолчанию для ЛДСП корпуса и МДФ фасада); заказчик или мебельщик подтверждает до раскроя.

	Лист	№ док.	Подпись	Дата	Проект: Квартира 65 м²			
Дизайнер	Кырлан А.С.			14.11.26	Ведомости изделий, техники и фурнитуры	Стадия	Лист	Листов
Проверил						П	26	105
Н. контр.								
Утв.								


Фрагмент 1. Кухня-гостиная, пом. 3 (М 1:25)

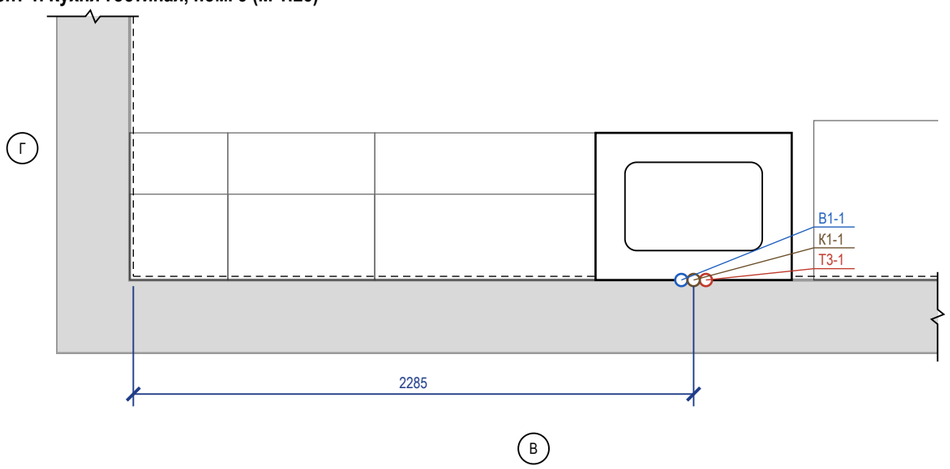

Фрагмент 2. Санузел, пом. 6 (М 1:25)

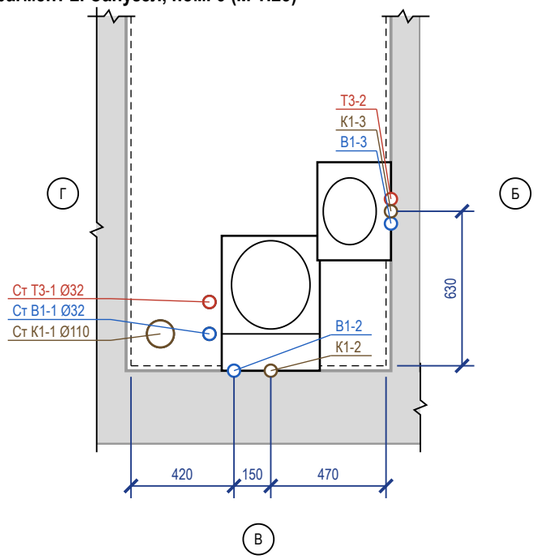

Фрагмент 3. Ванная, пом. 7 (М 1:25)

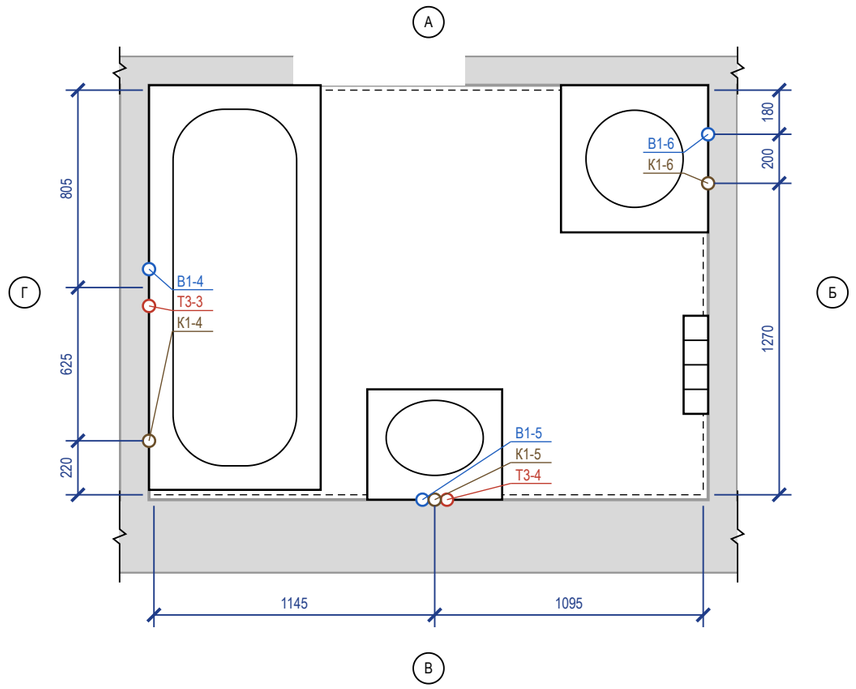

Ведомость привязок выводов

Код	Прибор	Ø	H, мм	Привязка от чист. стен, мм	Прим.
B1-1	С-01 мойка кухонная	½"	550	ст. В: 2235 от Г	межос. 100
Т3-1	—"	½"	550	ст. В: 2335 от Г	межос. 100
К1-1	—"	Ø50	400	ст. В: 2285 от Г	
B1-2	С-02 унитаз подвесной	½"	1000	ст. В: 420 от Г	в раме инсталляции
К1-2	—"	Ø110	220	ст. В: 470 от Б	
B1-3	С-03 умывальник	½"	550	ст. Б: 580 от В	межос. 100
Т3-2	—"	½"	550	ст. Б: 680 от В	межос. 100
К1-3	—"	Ø50	500	ст. Б: 630 от В	
B1-4	С-04 ванна	½"	800	ст. Г: 730 от А	межос. 150
Т3-3	—"	½"	800	ст. Г: 770 от В	межос. 150
К1-4	—"	Ø50	50	ст. Г: 220 от В	
B1-5	С-05 умывальник	½"	550	ст. В: 1095 от Г	межос. 100
Т3-4	—"	½"	550	ст. В: 1045 от Б	межос. 100
К1-5	—"	Ø50	500	ст. В: 1095 от Б	
B1-6	ОБ-02 стиральная машина	½"	800	ст. Б: 180 от А	кран машины
К1-6	—"	Ø50	600	ст. Б: 380 от А	

Условные обозначения

- вывод В1 (код — в ведомости привязок)
- вывод Т3 (код — в ведомости привязок)
- вывод К1 (код — в ведомости привязок)
- сантехприбор по расстановке (габарит модели)
- чистовая поверхность стены (от неё привязки)
- стояк «Ст К1-N / Ст В1-N» (ГОСТ 21.601), Ø мм
- линия обрыва (граница фрагмента)
- А — обозначение стены А–Г (как на развёртках)


Примечания

1. Привязки выводов даны от чистовых поверхностей стен (облицовка на сторону: кухня-гостиная — 15 мм (по данным); санузел — 20 мм (по данным); ванная — 20 мм (по данным)); эти же грани — на развёртках и в раскладке плитки. Высоты — от чистого пола помещения.
2. До черновой разводки сверить по паспорту выбранного прибора (смеситель, инсталляция, сифон).
3. Горячая вода (Т3) — слева от холодной (В1), если смотреть на прибор. Допуск установки выводов: ±5 мм в группе, ±20 мм у отдельно стоящих.
4. Расчёт систем водоснабжения и канализации и подбор оборудования выполняет проектная организация; лист задаёт места и высоты выводов.
5. Стояки в коробах/шахтах не замоноличивать; стояк К1 в коробе — звукоизоляция стояка в коробе без жёсткого контакта с трубой; к арматуре и ревизиям — люк не меньше 300×400.


	Лист	№ док.	Подпись	Дата	Проект: Квартира 65 м²	М 1:25
Дизайнер	Кырлан А.С.			14.11.26		
Проверил					План выводов сантехники	Стадия: П; Лист: 27; Листов: 105
Н. контр.						
Утв.						

выпуск 14.11.2026 № 3aed0ef730 · стр. 27 из 105


План квартиры (М 1:400)

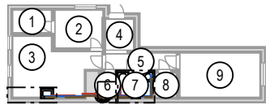


Фр. 1. Кухня-гостиная (М 1:25)

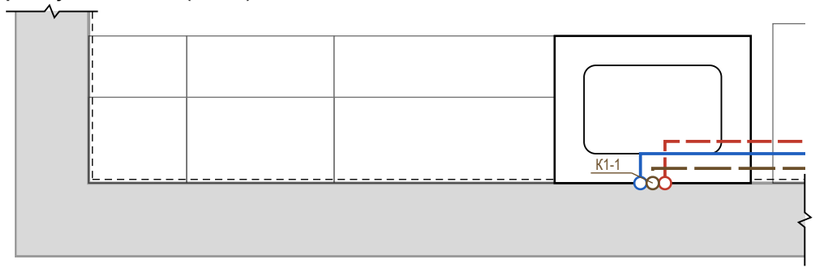

Фр. 2. Санузел (М 1:25)

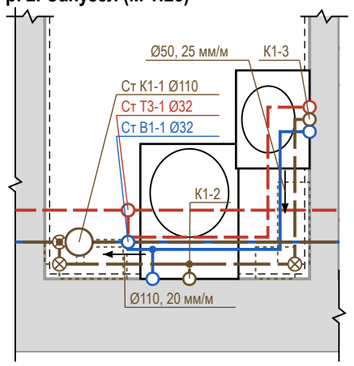

Фр. 3. Ванная (М 1:25)

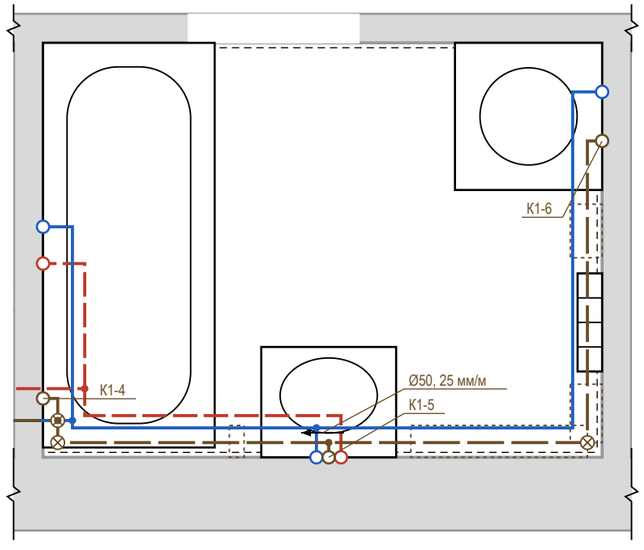

Условные обозначения


- В1 — водопровод хозяйственно-питьевой (ХВС), PP-R Ø20
- Т3 — горячее водоснабжение, подача (ГВС), PP-R Ø20
- К1 — канализация бытовая
- направление уклона К1 / пола: Ø, мм на 1 м
- ревизия (прочистка) К1 — доступ сохранить
- тройник (ответвление к прибору)
- короб К1 над чистым полом (ГКЛВ под плитку)
- вывод В1 (код — в ведомости привязок)
- вывод Т3 (код — в ведомости привязок)
- вывод К1 (код — в ведомости привязок)
- сантехприбор по расстановке (габарит модели)
- стояк «Ст К1-N / Ст В1-N» (ГОСТ 21.601), Ø мм
- линия обрыва (граница фрагмента)
- граница фрагмента на плане (Фр. N)

Профиль выпусков К1 (до врезки в стояк)

Выпуск	Прибор	Ø	L, м	i, мм/м	Δh, мм	Прокладка, мм
К1-2	С-02 унитаз подвесной	Ø110	0,76	20	15	короб 160×140
К1-6	ОБ-02 стиральная машина	Ø50	4,66	25	117	короб 200×110
К1-1	С-01 мойка кухонная	Ø50	3,70	25	93	над полом за приборами
К1-5	С-05 умывальник	Ø50	2,38	25	59	над полом за приборами
К1-3	С-03 умывальник	Ø50	1,78	25	45	короб 130×110
К1-4	С-04 ванна	Ø50	1,27	25	32	над полом за приборами

Короб h×b: h — от чистого пола, b — от чистовой стены. Стяжка 90 мм — лист полов.

Узел ввода В1, Т3 (по данным, без масштаба)

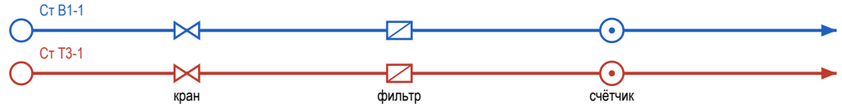


⊗ Ст К1-1: ревизия на стояке — люк в коробе

Примечания

1. Трассы принципиальные, построены от стояков вдоль стен помещений; фактическое положение фиксируется исполнительной схемой с привязками (фото с рулеткой) до закрытия.
2. Уклон К1 не менее 1/d и не более 150 мм/м (СП 30.13330.2020, п. 19.1), приняты практические уклоны; поворот — двумя отводами 45°, ревизия после поворота, доступ сохранить. Стояк К1 в коробе — звукоизоляция стояка в коробе, без жёсткого контакта короба с трубой.
3. Решение по К1: стяжка 90 мм не укрывает трубы (нужно Ø + Δh + 45 мм) — выпуски идут над чистым полом вдоль стен: К1-1, К1-5, К1-4 — за приборами и в раме инсталляции; К1-2, К1-6, К1-3 — в коробе ГКЛВ под плитку (размеры в профиле). Короба — на развёртках; отметку низа врезки в стояк замерить до черновых работ.
4. Отводы К1-6 (4,7 м) длиннее 4 м без вентиляции — у прибора воздушный клапан Ø50 в доступном месте (за люком или в тумбе) либо вентилируемый отвод (EN 12056-2, табл. 4), подбор — проектная организация.
5. Узел ввода В1, Т3 — по данным проекта: кран → фильтр → счётчик. Доступ к арматуре — через люк не меньше 300×400. Водопровод — в штробе стен или в коробах; трубы испытать давлением до закрытия (акт скрытых работ).
6. Расчёт систем, диаметры магистралей и подбор оборудования выполняет проектная организация; врезка и перенос стояков — по согласованию с управляющей организацией. Арматуру и привязки сверить по паспортам приборов.
7. Ведомость выводов (код, прибор, высота, привязка) — лист 27; на схеме — только коды.

	Лист	№ док.	Подпись	Дата	Проект: Квартира 65 м²			
Дизайнер	Кырлан А.С.			14.11.26				
Проверил					Схема разводки водопровода и канализации	Стадия	Лист	Листов
Н. контр.								
Утв.						П	28	105

Схема В1 (М 1:50)

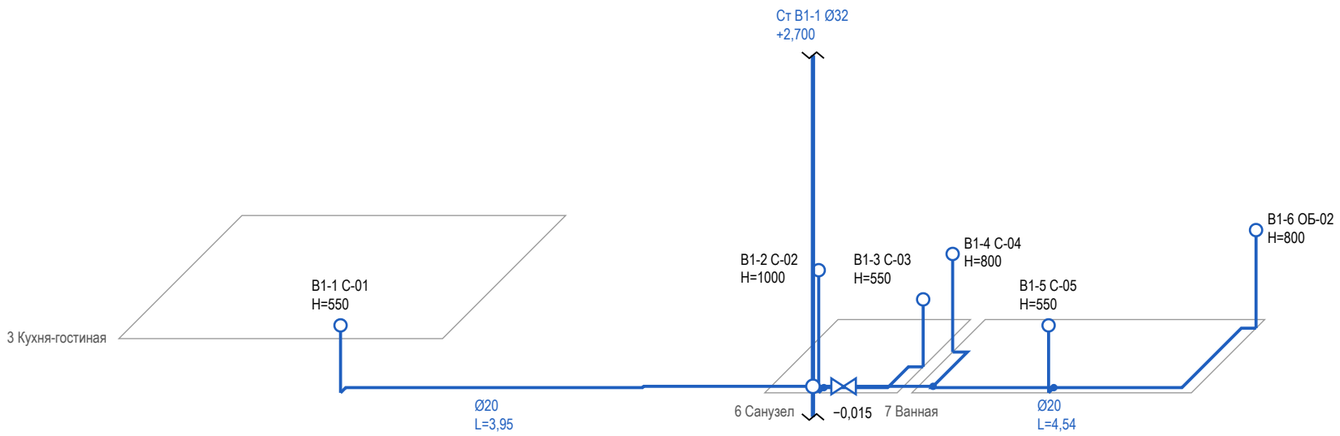

Ведомость выводов В1

Код	Прибор	H, мм	Ø, мм	Трасса, м
В1-6	ОБ-02 стиральная машина	800	20	4,54
В1-1	С-01 мойка кухонная	550	20	3,95
В1-5	С-05 умывальник	550	20	0,12
В1-4	С-04 ванна	800	20	0,91
В1-3	С-03 умывальник	550	20	1,25
В1-2	С-02 унитаз подвесной	1000	20	0,12

Условные обозначения

- В1 — водопровод хозяйственно-питьевой (ХВС), PP-R Ø20
- вывод В1 (код — в ведомости привязок)
- стояк «Ст К1-N / Ст В1-N» (ГОСТ 21.601), Ø мм
- стояк в плане (на отметке пола); вертикаль — стояк по высоте, разрыв — перекрытие
- тройник (ответвление к прибору)
- кран шаровой

Примечания


1. Схема В1 построена по тем же трассам, что план разводки: положение в плане сохранено, глубина — в масштабе ×0,5. Трассы принципиальные; фактическое положение фиксируется исполнительной схемой до закрытия.
2. Высоты H — от чистого пола помещения, мм. Прокладка магистрали В1 по данным: в стяжке пола, в стяжке пола, выше плиты перекрытия; отметка трасс — по пирогу пола.
3. Узел ввода В1 (кран, фильтр, счётчик, обратный клапан, кран) — на схеме разводки; состав узла ввода — по согласованию. Кран шаровой — на первом участке от стояка.
4. Трубы испытать давлением до закрытия (акт скрытых работ, опрессовка по СП 73.13330.2016).
5. Диаметры, высоты выводов и места кранов — по паспортам выбранных приборов и расчёту проектной организации.
6. Расчёт систем, диаметры магистралей и подбор оборудования выполняет проектная организация.

	Лист	№ док.	Подпись	Дата
Дизайнер	Кырлан А.С.			14.11.26
Проверил				
Н. контр.				
Утв.				

Проект: Квартира 65 м² — **М 1:50**

Аксонометрическая схема В1 (холодное водоснабжение)	Стадия	Лист	Листов
	П	29	105

Схема Т3 (М 1:50)

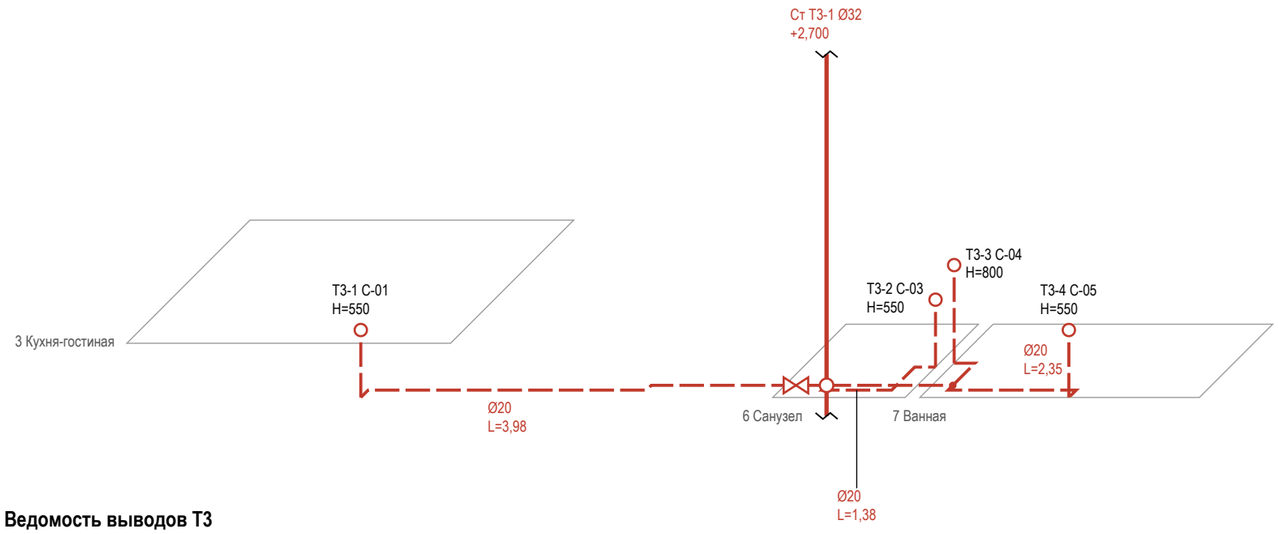

Ведомость выводов Т3

Код	Прибор	H, мм	Ø, мм	Трасса, м
Т3-1	С-01 мойка кухонная	550	20	3,98
Т3-4	С-05 умывальник	550	20	2,35
Т3-3	С-04 ванна	800	20	0,68
Т3-2	С-03 умывальник	550	20	1,38

Условные обозначения


- Т3 — горячее водоснабжение, подача (ГВС), PP-R Ø20
- вывод Т3 (код — в ведомости привязок)
- стояк «Ст К1-N / Ст В1-N» (ГОСТ 21.601), Ø мм
- стояк в плане (на отметке пола); вертикаль — стояк по высоте, разрыв — перекрытие
- тройник (ответвление к прибору)
- кран шаровой

Примечания

1. Схема Т3 построена по тем же трассам, что план разводки: положение в плане сохранено, глубина — в масштабе ×0,5. Трассы принципиальные; фактическое положение фиксируется исполнительной схемой до закрытия.
2. Высоты H — от чистого пола помещения, мм. Прокладка магистрали Т3 по данным: в стяжке пола, в стяжке пола, выше плиты перекрытия; отметка трасс — по пирогу пола.
3. Узел ввода Т3 (кран, фильтр, счётчик, обратный клапан, кран) — на схеме разводки; состав узла ввода — по согласованию. Кран шаровой — на первом участке от стояка.
4. Циркуляция ГВС в данных не задана — циркуляционного трубопровода на схеме нет.
5. Трубы испытать давлением до закрытия (акт скрытых работ, опрессовка по СП 73.13330.2016).
6. Диаметры, высоты выводов и места кранов — по паспортам выбранных приборов и расчёту проектной организации.
7. Расчёт систем, диаметры магистралей и подбор оборудования выполняет проектная организация.

	Лист	№ док.	Подпись	Дата	Проект: Квартира 65 м²			М 1:50
Дизайнер	Кырлан А.С.			14.11.26	Аксонометрическая схема Т3 (горячее водоснабжение)	Стадия	Лист	Листов
Проверил						П	30	105
Н. контр.								
Утв.								

Схема К1 (М 1:50)

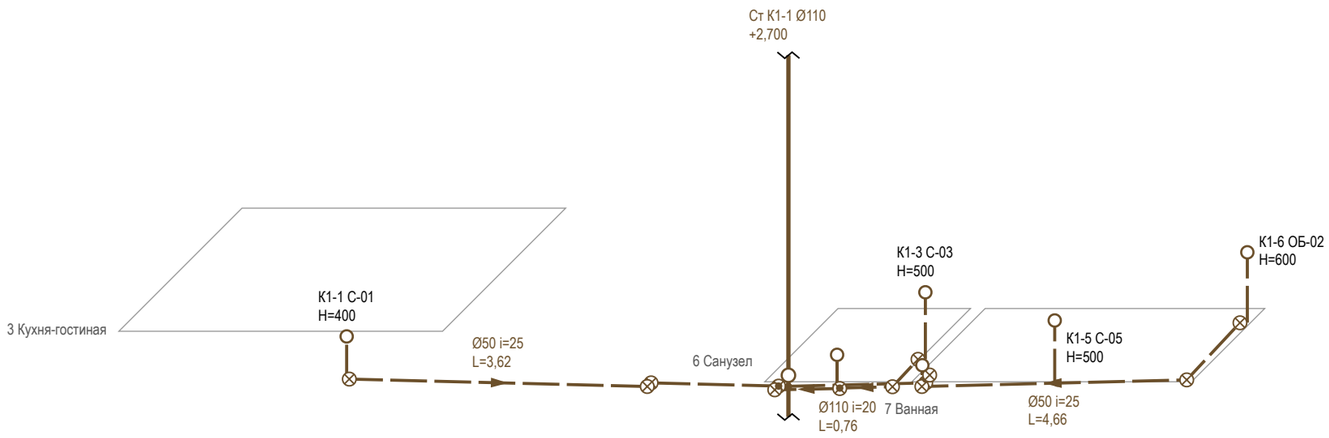

Ведомость выводов К1

Код	Прибор	H, мм	Ø, i	Трасса, м
К1-2	С-02 унитаз подвесной	220	110 i=20	0,76
К1-6	ОБ-02 стиральная машина	600	50 i=25	4,66
К1-1	С-01 мойка кухонная	400	50 i=25	3,62
К1-5	С-05 умывальник	500	50 i=25	0,06
К1-3	С-03 умывальник	500	50 i=25	1,08
К1-4	С-04 ванна	50	50 i=25	0,15

Условные обозначения


- К1 — канализация бытовая
- вывод К1 (код — в ведомости привязок)
- стояк «Ст К1-N / Ст В1-N» (ГОСТ 21.601), Ø мм
- стояк в плане (на отметке пола); вертикаль — стояк по высоте, разрыв — перекрытие
- направление уклона К1 / пола: Ø, мм на 1 м
- ⊗ ревизия (прочистка) К1 — доступ сохранить
- • тройник (ответвление к прибору)

Примечания

1. Схема К1 построена по тем же трассам, что план разводки: положение в плане сохранено, глубина — в масштабе ×0,5. Трассы принципиальные; фактическое положение фиксируется исполнительной схемой до закрытия.
2. Отметки — от плиты перекрытия: низ трубы у врезки в стояк — отметка из данных выпуска, к прибору труба поднимается на уклон i, мм/м (уклон не менее 1/d и не более 150 мм/м, СП 30.13330.2020, п. 19.1); чистый пол — выше плиты на стяжку (высота пирога пола). Высота выпуска прибора H — от чистого пола.
3. Ревизия — на повороте и в начале участка; стояк К1 в коробе с люком — звукоизоляция стояка в коробе; поворот — двумя отводами 45°.
4. Трубы испытать давлением до закрытия (акт скрытых работ, опрессовка по СП 73.13330.2016).
5. Диаметры, высоты выводов и места кранов — по паспортам выбранных приборов и расчёту проектной организации.
6. Расчёт систем, диаметры магистралей и подбор оборудования выполняет проектная организация.

	Лист	№ док.	Подпись	Дата	Проект: Квартира 65 м²	М 1:50		
Дизайнер	Кырлан А.С.			14.11.26	Аксонометрическая схема К1 (канализация)	Стадия	Лист	Листов
Проверил						П	31	105
Н. контр.								
Утв.								

Стена В (М 1:20)

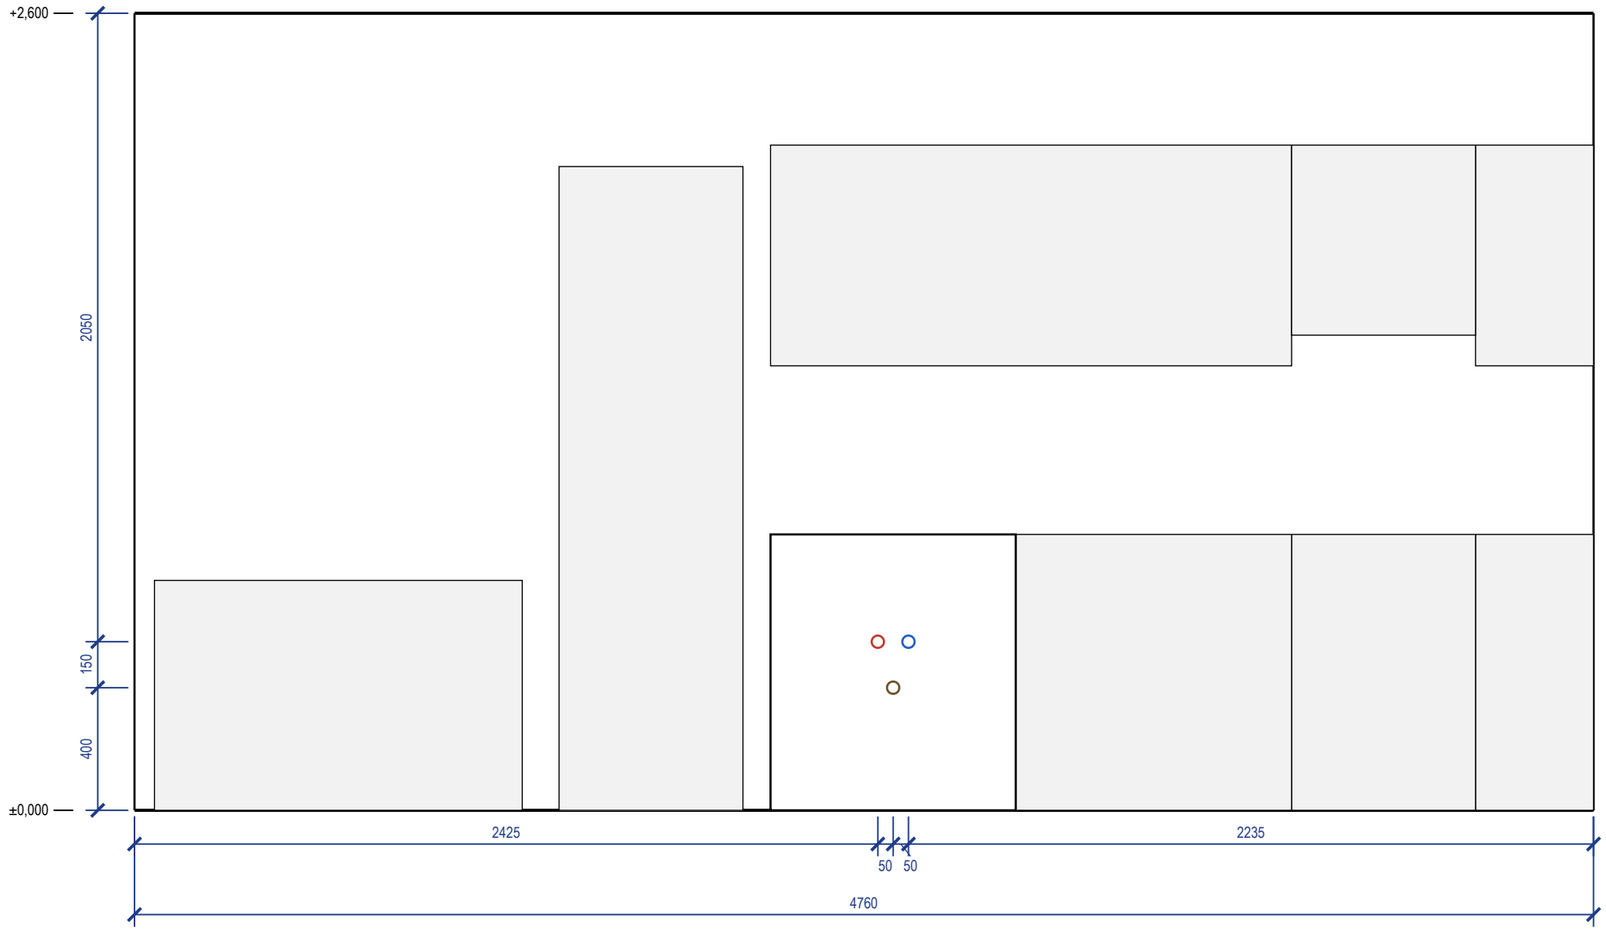

Ведомость привязок выводов (от чистого пола и угла)

Код	Прибор	Ø	H, мм	Привязка, мм
В1-1	С-01 мойка кухонная	½"	550	ст. В: 2525 от лев. угла
Т3-1	С-01 мойка кухонная	½"	550	ст. В: 2425 от лев. угла
К1-1	С-01 мойка кухонная	Ø50	400	ст. В: 2475 от лев. угла

Условные обозначения


- вывод В1 (код — в ведомости привязок)
- вывод Т3 (код — в ведомости привязок)
- вывод К1 (код — в ведомости привязок)
- сантехприбор по расстановке (габарит модели)
- дверной проём; окно — сплошной контур

Примечания


1. Габариты и высоты приборов, межосевые смесителей и места кранов — по паспортам выбранных приборов, сверяются до разметки стен.
2. Высоты H — от чистого пола помещения, мм; отметка чистого пола и потолка — у левого края вида (от ±0,000 объекта). Привязки — от левого чистового угла вида (облицовка стен вычтена), как на развёртках стен.
3. Ревизионные люки (арматура и ревизии у С-01 300×400, стена В у С-01, предложение): привязка к углу — по раскладке плитки, подтверждается обмером.
4. Ревизионные люки к арматуре и ревизиям в данных не заданы: место и размер не определены (записи реестра нет).
5. Мойка, ПММ и фильтр — выводы в шкафу мойки; диаметры и положение сифона и кранов сверить по паспортам приборов и чертежам модуля.
6. Часть подписей выводов не уместилась у знака: коды и высоты — в ведомости привязок.
7. Расчёт систем водоснабжения и канализации и подбор оборудования выполняет проектная организация; лист задаёт места и высоты выводов.

	Лист	№ док.	Подпись	Дата	Проект: Квартира 65 м²			М 1:20
Дизайнер	Кырлан А.С.			14.11.26	Развёртки мокрых зон: выводы ВК. Кухня-гостиная	Стадия	Лист	Листов
Проверил						П	32	105
Н. контр.								
Утв.								

Стена Б (М 1:20)

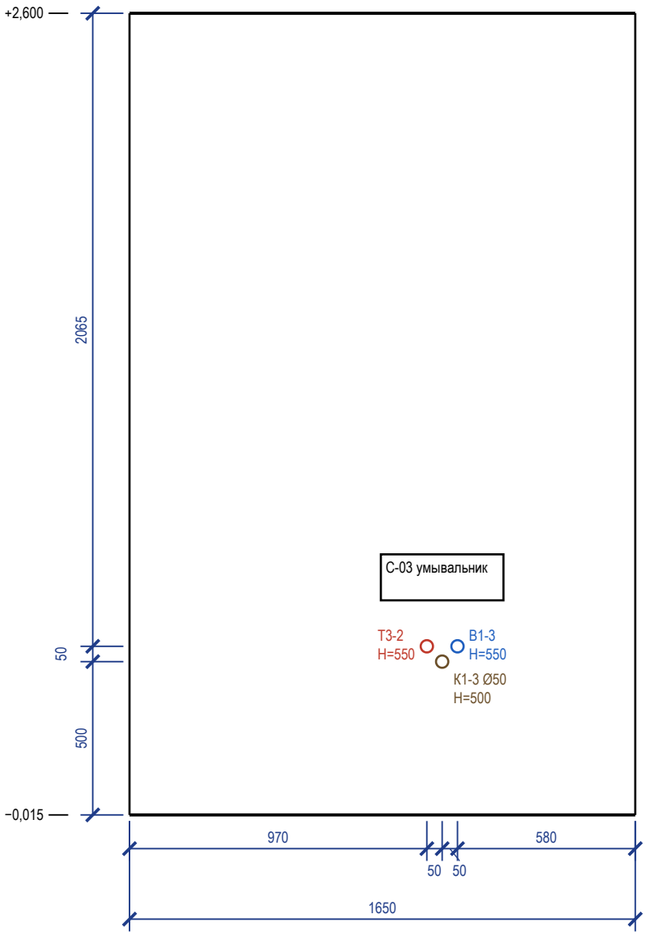

Стена В (М 1:20)

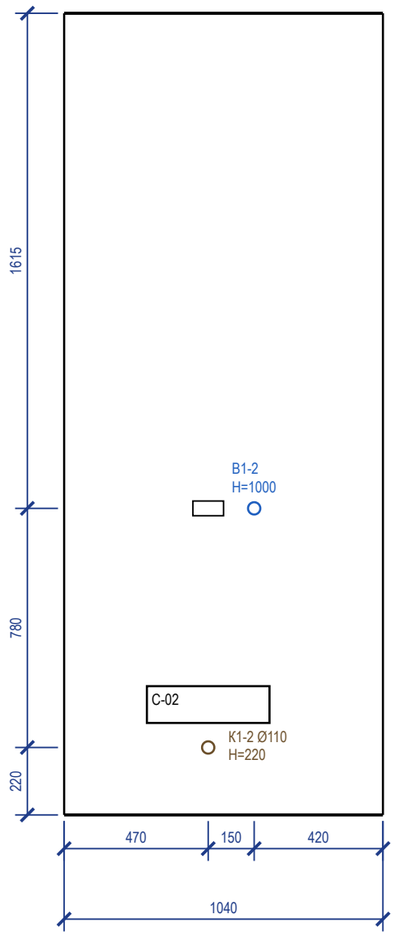

Ведомость привязок выводов (от чистого пола и угла)

Код	Прибор	Ø	H, мм	Привязка, мм
B1-3	C-03 умывальник	½"	550	ст. Б: 1070 от лев. угла
T3-2	C-03 умывальник	½"	550	ст. Б: 970 от лев. угла
K1-3	C-03 умывальник	Ø50	500	ст. Б: 1020 от лев. угла
B1-2	C-02 унитаз подвесной	½"	1000	ст. В: 620 от лев. угла
K1-2	C-02 унитаз подвесной	Ø110	220	ст. В: 470 от лев. угла

Условные обозначения

- вывод B1 (код — в ведомости привязок)
- вывод T3 (код — в ведомости привязок)
- вывод K1 (код — в ведомости привязок)
- сантехприбор по расстановке (габарит модели)
- дверной проём; окно — сплошной контур
- кнопка смыва инсталляции (H — по данным прибора)


Примечания

1. Габариты и высоты приборов, межосевые смесителей и места кранов — по паспортам выбранных приборов, сверяются до разметки стен.
2. Высоты H — от чистого пола помещения, мм; отметка чистого пола и потолка — у левого края вида (от ±0,000 объекта). Привязки — от левого чистового угла вида (облицовка стен вычтена), как на развёртках стен.
3. Кнопка смыва C-02 — H=1000 (по данным прибора).
4. Стояки в помещении: Ст K1-1 Ø110, Ст B1-1 Ø32, Ст T3-1 Ø32 — положение на плане выводов; выводы подключаются к ним по схеме разводки.
5. Ревизионные люки (арматура и ревизии у C-02 300×400, стена В у C-02, предложение): привязка к углу — по раскладке плитки, подтверждается обмером.
6. Ревизионные люки к арматуре и ревизиям в данных не заданы: место и размер не определены (записи реестра нет).
7. Расчёт систем водоснабжения и канализации и подбор оборудования выполняет проектная организация; лист задаёт места и высоты выводов.


	Лист	№ док.	Подпись	Дата	Проект: Квартира 65 м²			М 1:20
Дизайнер	Кырлан А.С.			14.11.26	Развёртки мокрых зон: выводы ВК. Санузел	Стадия	Лист	Листов
Проверил						П	33	105
Н. контр.								
Утв.								

выпуск 14.11.2026 № 3aed0ef730 · стр. 33 из 105


Стена Б (М 1:20)

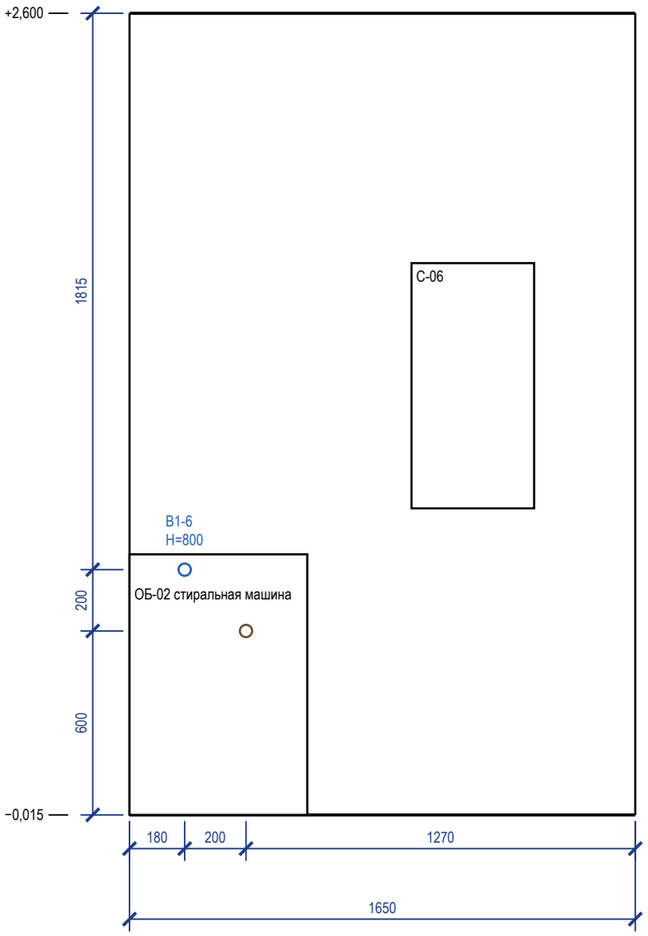

Стена В (М 1:20)

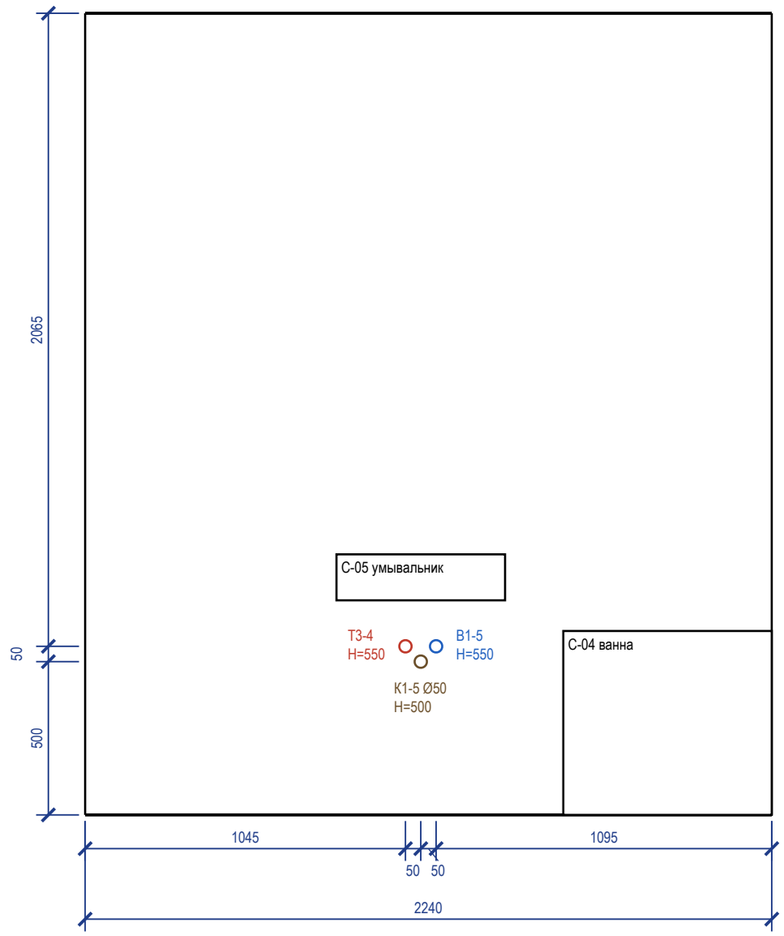

Стена Г (М 1:20)

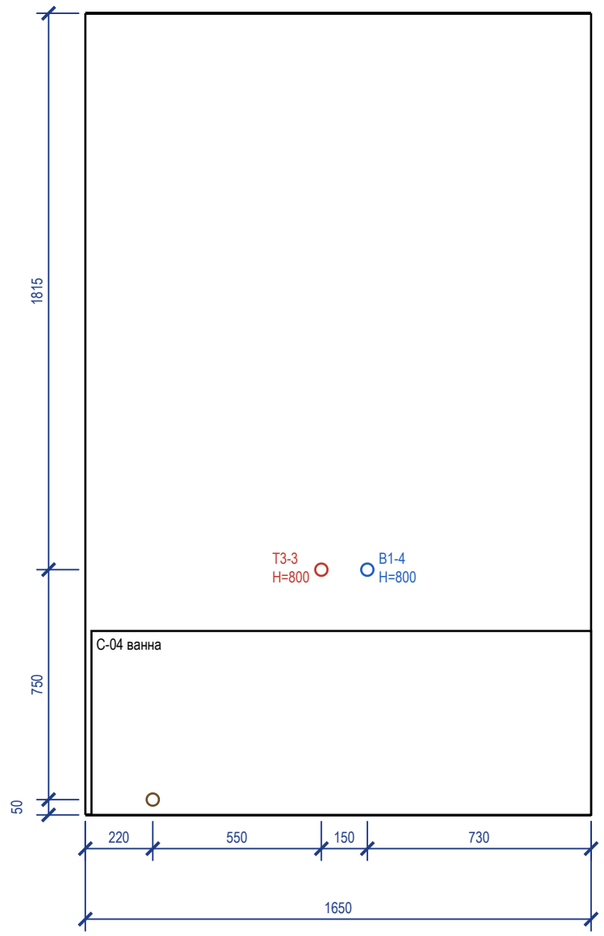

Ведомость привязок выводов (от чистого пола и угла)

Код	Прибор	Ø	H, мм	Привязка, мм
В1-6	ОБ-02 стиральная машина	½"	800	ст. Б: 180 от лев. угла
К1-6	ОБ-02 стиральная машина	Ø50	600	ст. Б: 380 от лев. угла
В1-5	С-05 умывальник	½"	550	ст. В: 1145 от лев. угла
Т3-4	С-05 умывальник	½"	550	ст. В: 1045 от лев. угла

Ведомость привязок (продолжение)

Код	Прибор	Ø	H, мм	Привязка, мм
К1-5	С-05 умывальник	Ø50	500	ст. В: 1095 от лев. угла
В1-4	С-04 ванна	½"	800	ст. Г: 920 от лев. угла
Т3-3	С-04 ванна	½"	800	ст. Г: 770 от лев. угла
К1-4	С-04 ванна	Ø50	50	ст. Г: 220 от лев. угла

Условные обозначения

- вывод В1 (код — в ведомости привязок)
- вывод Т3 (код — в ведомости привязок)
- вывод К1 (код — в ведомости привязок)
- сантехприбор по расстановке (габарит модели)
- дверной проём; окно — сплошной контур

Примечания

1. Габариты и высоты приборов, межосевые смесителей и места кранов — по паспортам выбранных приборов, сверяются до разметки стен.
2. Высоты H — от чистого пола помещения, мм; отметка чистого пола и потолка — у левого края вида (от ±0,000 объекта). Привязки — от левого чистового угла вида (облицовка стен вычтена), как на развёртках стен.
3. Ревизионные люки (арматура и ревизии у С-04 300×400, стена Г у С-04, предложение): привязка к углу — по раскладке плитки, подтверждается обмером.
4. Ревизионные люки к арматуре и ревизиям в данных не заданы: место и размер не определены (записи реестра нет).
5. Часть подписей выводов не уместилась у знака: коды и высоты — в ведомости привязок.
6. Стены А: выводов В1, Т3, К1 нет — развёртка не строится (иначе лист-продолжение); приборы и проёмы этих стен — на плане выводов и развёртках стен чертёжника.
7. Расчёт систем водоснабжения и канализации и подбор оборудования выполняет проектная организация; лист задаёт места и высоты выводов.

	Лист	№ док.	Подпись	Дата
Дизайнер	Кырлан А.С.			14.11.26
Проверил				
Н. контр.				
Утв.				

Проект: Квартира 65 м² — М 1:20

Развёртки мокрых зон: выводы ВК. Ванная

Стадия	Лист	Листов
П	34	105


выпуск 14.11.2026 № 3aed0ef730 · стр. 34 из 105

Поз.	Наименование и техническая характеристика	Тип, марка, обозначение документа	Код продукции	Поставщик	Ед. изм.	Кол.	Масса 1 ед., кг	Примечание
	Санитарные приборы							
1	Ванна встраиваемая акриловая 1650×700 мм, с каркасом, экраном и отверстием слив-перелив	Ravak Classic C541000000		выбор заказчика	шт	1		С-04
2	Унитаз подвесной безободковый, с сиденьем микролифт, крепёж и звукоизолирующая прокладка	Jacob Delafon Struktura EDF102-00		выбор заказчика	шт	1		С-02
3	Инсталляция для подвесного унитаза: рама высотой 1120 мм, бачок, клавиша смыва (ось клавиши 1050 мм от чистого пола)	аналог		выбор заказчика	шт	1		С-02; короб ГКЛВ
4	Умывальник подвесной 400×300 мм, с отверстием под смеситель и переливом	Roca The Gap 7.3274.7.400.0		выбор заказчика	шт	1		С-03
5	Умывальник подвесной 550×450 мм, с отверстием под смеситель и переливом	Roca The Gap 7.3274.7.400.0		выбор заказчика	шт	1		С-05
6	Мойка кухонная 700×480 мм, с переливом	мойка врезная 700×480 в шкафу М-11		с кухонной мебелью	шт	1		С-01
7	Полотенцесушитель электрический, IP44, с терморегулятором	аналог		выбор заказчика	шт	1		С-06
	Смесители, сифоны и арматура приборов							
8	Смеситель для ванны настенный однорычажный, межосевое 150 мм, с душевым набором (лейка, шланг, держатель)	аналог		выбор заказчика	шт	1		С-04
9	Смеситель для умывальника однорычажный, с донным клапаном	аналог		выбор заказчика	шт	2		С-03, С-05
10	Смеситель кухонный однорычажный, высокий излив	аналог		выбор заказчика	шт	1		С-01
11	Обвязка ванны слив-перелив Ø40/50 с сифоном	аналог		выбор заказчика	шт	1		С-04
12	Сифон для умывальника бутылочный Ø32/40–50, с гофрой к выпуску	аналог		выбор заказчика	шт	2		С-03, С-05
13	Сифон для мойки Ø40/50	аналог		выбор заказчика	шт	1		С-01
14	Сифон для стиральной машины встраиваемый в стену Ø50, с обратным клапаном	аналог		выбор заказчика	шт	1		ОБ-02
15	Кран угловой ½"×½" с гибкой подводкой 40 см (умывальники, мойка)	аналог		выбор заказчика	шт	6		по 2 на прибор
16	Кран шаровой угловой ½"×¾" для подключения стиральной и посудомоечной машины	аналог		выбор заказчика	шт	1		ОБ-02
	Трубопроводы							
17	Труба полипропиленовая PP-R PN20 Ø20×3,4 (В1)	ГОСТ 32415-2013		выбор заказчика	м	17	0,17	10,9 + 4,3 + 10 %
18	Труба PP-R, армированная стекловолокном, PN20 Ø20×2,8 (Т3)	ГОСТ 32415-2013		выбор заказчика	м	12	0,15	8,4 + 2,5 + 10 %
19	Труба канализационная ПП Ø50 (К1)	ГОСТ 32414-2013		выбор заказчика	м	13		9,6 + 2,0 + 10 %
20	Труба канализационная ПП Ø110 (К1)	ГОСТ 32414-2013		выбор заказчика	м	1,5		0,8 + 0,2 + 10 %
	Фасонные части и выводы							
21	Отвод канализационный ПП 45° Ø50	ГОСТ 32414-2013		выбор заказчика	шт	20		2 шт. на поворот
22	Отвод канализационный ПП 45° Ø110	ГОСТ 32414-2013		выбор заказчика	шт	6		2 шт. на поворот
23	Тройник канализационный ПП 45° (врезки ветвей)	ГОСТ 32414-2013		выбор заказчика	шт	5		
24	Ревизия канализационная ПП (после поворота трассы)	ГОСТ 32414-2013		выбор заказчика	шт	8		доступ сохранить
25	Фитинги PP-R Ø20: тройники, угольники 90° (ветви и повороты В1, Т3)	ГОСТ 32415-2013		выбор заказчика	шт	29		
26	Водорозетка PP-R Ø20×½" настенная, с креплением	ГОСТ 32415-2013		выбор заказчика	шт	10		коды — лист выводов
	Узлы ввода, люки, короба							
27	Кран шаровой латунный Ду15 PN16 (отключение ввода)	аналог		выбор заказчика	шт	2		Ст В1-1, Ст Т3-1
28	Фильтр сетчатый косой Ду15	аналог		выбор заказчика	шт	2		
29	Счётчик воды крыльчатый Ду15 (ХВ, ГВ), с поверкой	аналог		выбор заказчика	шт	2		пломба УК
30	Клапан обратный Ду15	аналог		выбор заказчика	шт	2		
31	Люк ревизионный нажимной под плитку 300×400 мм	аналог		выбор заказчика	шт	3		к стоякам и арматуре
32	Звукоизоляция стояка К1 в коробе: рулонный звукоизоляционный материал ≥ 10 мм, обмотка стояка на высоту этажа	аналог		выбор заказчика	м	2,7		Ст К1-1
33	Короб К1 над полом: профиль ПН/ПС, ГКЛВ 12,5 мм под плитку	аналог		выбор заказчика	м	2,9		сечение — лист разводки

Примечания

1. Форма 1 ГОСТ 21.110-2013, ширины граф изменены по п. 4.1. «Аналог» — аналог по характеристикам: модели внести до черновых работ, привязки выводов сверить по паспортам.
2. Бытовая техника не входит (показана арматура подключения), мойка — в комплекте кухни (марка — модуля кухни, как у столяра). Длины труб — трасса листа разводки + подъёмы + 10 %.
3. Стояк К1 в коробе — звукоизоляция стояка в коробе без жёсткого контакта короба с трубой.
4. Расчёт систем водоснабжения и канализации, диаметры магистралей и подбор оборудования выполняет проектная организация.

	Лист	№ док.	Подпись	Дата	Проект: Квартира 65 м²			
Дизайнер	Кырлан А.С.			14.11.26	Спецификация сантехнического оборудования	Стадия	Лист	Листов
Проверил						П	35	105
Н. контр.								
Утв.								

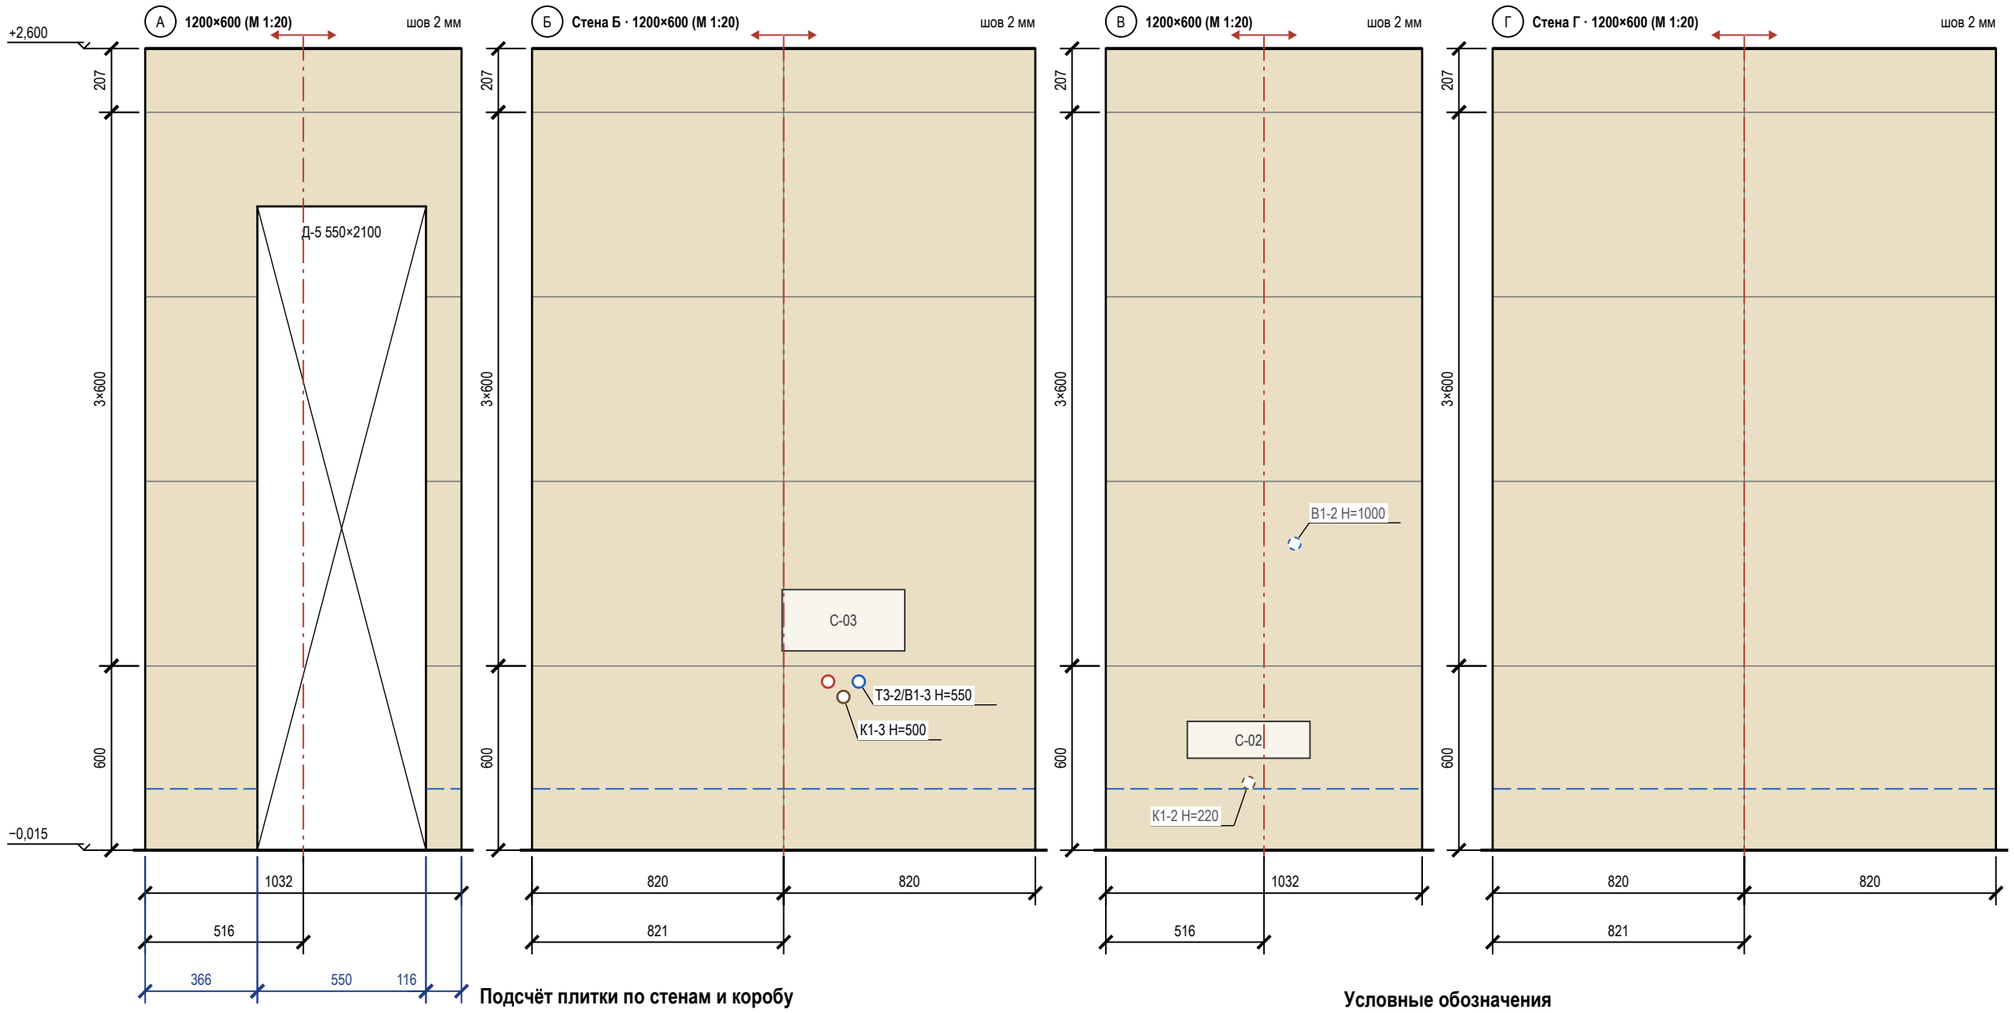

Подсчёт плитки по стенам и коробу

Поверхность	L × H, мм	S, м²	Целых	Подр.	С запасом	Подрезки: край / верх, мм
стена А	1032 × 2615	1,67	0	5	6	1032; 207
стена Б	1642 × 2615	4,42	0	10	11	820 / 820; 207
стена В	1032 × 2615	2,82	0	5	6	1032; 207
стена Г	1642 × 2615	4,42	0	10	11	820 / 820; 207
Итого		**13,33**	**0**	**30**	**34**	

Условные обозначения

- плитка целая; тонкая линия — шов
- плитка с подрезкой (размер — на цепочке)
- ось старта; стрелки — направление укладки
- верх гидроизоляции: 200 от ЧП, в мокрой зоне — «до …»
- проём — не облицовывается
- сантехприбор: габарит, высота по практике
- вывод В1 (код — в ведомости привязок)
- вывод Т3 (код — в ведомости привязок)
- вывод К1 (код — в ведомости привязок)
- вывод за прибором / в коробе (не на сетке)
- отметка уровня, м: ±0,000 — чистый пол жилых помещений
- низ потолка; серая полоса — стена без плитки
- (А) обозначение стены А–Г (как на развёртках)

Примечания

1. Вид изнутри, стены по часовой стрелке А → Г. Высоты — от чистого пола (−0,015), отметки — от ±0,000. Раскладка от чистовых размеров (штукатурка 10 + клей 5 + плитка 9 мм), подрезки чистые; старт — от оси стены, ряды от пола целыми.
2. Облицовка до потолка (+2,600).
3. Открытые выводы и электроточки — на шве или в центре плитки (допуск 10 мм; плитка от 900 мм по высоте — на шве или не ближе 60 мм к нему).
4. Выводы ВК стоят по оси прибора и с прибором не двигаются — привязки по «Плану выводов сантехники» без сдвига; вне сетки (Т3-2/В1-3, К1-3) — отверстие в плитке коронкой по той же привязке, плитку не сдвигать.
5. За приборами и в коробе (В1-2, К1-2) — штриховым кольцом.
6. Гидроизоляция: 200 мм от ЧП по периметру; углы — лентой; акт скрытых работ, пролив.


	Лист	№ док.	Подпись	Дата
Дизайнер	Кырлан А.С.			14.11.26
Проверил				
Н. контр.				
Утв.				

Проект: Квартира 65 м² — **М 1:20**

Раскладка плитки. Санузел. Развёртки стен

Стадия	Лист	Листов
П	36	105

выпуск 14.11.2026 № 3aed0ef730 · стр. 36 из 105

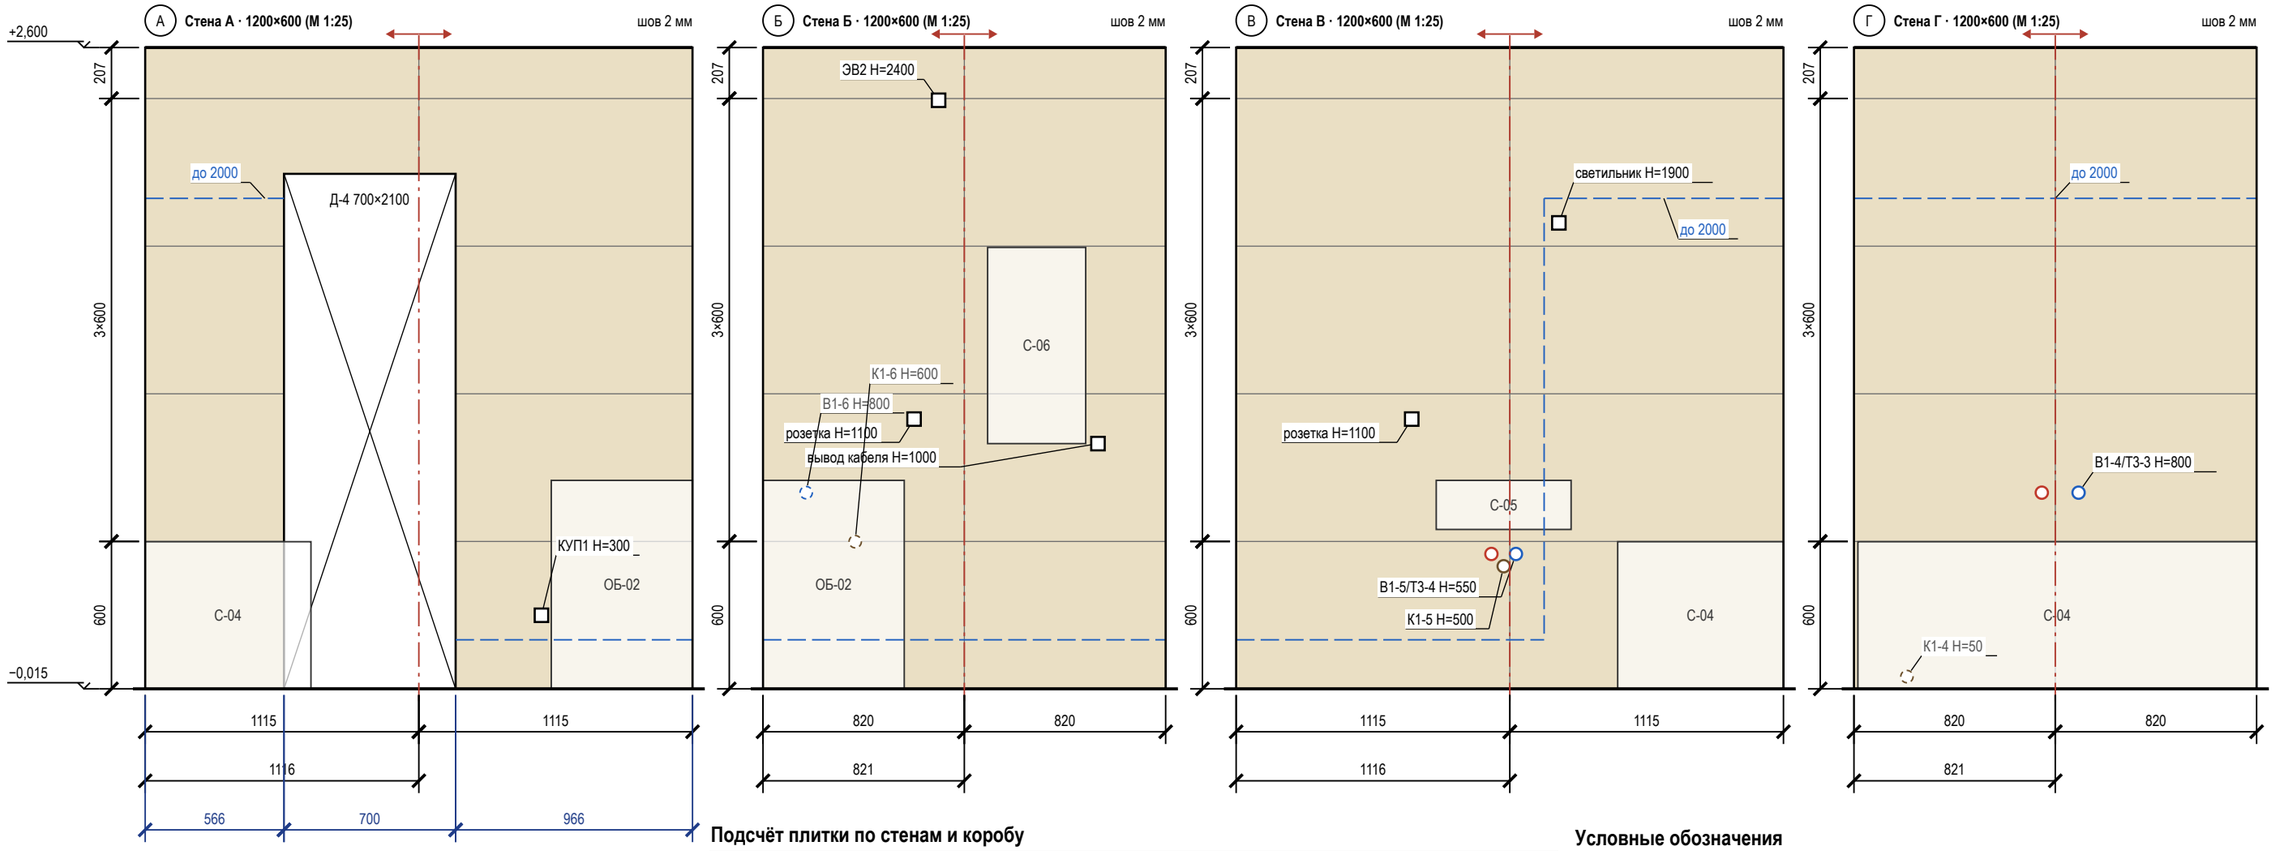

Подсчёт плитки по стенам и коробу

Поверхность	L × H, мм	S, м²	Целых	Подр.	С запасом	Подрезки: край / верх, мм
стена А	2232 × 2615	4,49	0	10	11	1115 / 1115; 207
стена Б	1642 × 2615	4,42	0	10	11	820 / 820; 207
стена В	2232 × 2615	5,96	0	10	11	1115 / 1115; 207
стена Г	1642 × 2615	4,42	0	10	11	820 / 820; 207
Итого		**19,29**	**0**	**40**	**44**	

Сдвиг точек под раскладку

Точка (ВК, ЭОМ)	Стена	Проект: от угла / Н	Под раскладку: от угла / Н	Сдвиг, мм
вывод кабеля	Б	1366 / 1000	1366 / 902	Н −98
розетка	Б	616 / 1100	616 / 1203	Н +103
розетка	В	716 / 1100	716 / 1203	Н +103
светильник	В	1316 / 1900	1316 / 1805	Н −95

Условные обозначения

- плитка целая; тонкая линия — шов
- плитка с подрезкой (размер — на цепочке)
- ось старта; стрелки — направление укладки
- верх гидроизоляции: 200 от ЧП, в мокрой зоне — «до …»
- проём — не облицовывается
- сантехприбор: габарит, высота по практике
- вывод В1 (код — в ведомости привязок)
- вывод Т3 (код — в ведомости привязок)
- вывод К1 (код — в ведомости привязок)
- вывод за прибором / в коробе (не на сетке)
- электроточка: марка и Н — по листам ЭОМ
- отметка уровня, м: ±0,000 — чистый пол жилых помещений
- низ потолка; серая полоса — стена без плитки
- (А) обозначение стены А–Г (как на развёртках)

Примечания

1. Вид изнутри, стены по часовой стрелке А → Г. Высоты — от чистого пола (−0,015), отметки — от ±0,000. Раскладка от чистовых размеров (штукатурка 10 + клей 5 + плитка 9 мм), подрезки чистые; старт — от оси стены, ряды от пола целыми.
2. Облицовка до потолка (+2,600).
3. Точки из таблицы сдвигов переносятся до черновой разводки (ЭОМ — по тем же числам).
4. Выводы ВК стоят по оси прибора и с прибором не двигаются — привязки по «Плану выводов сантехники» без сдвига; вне сетки (В1-5/Т3-4, К1-5, В1-4/Т3-3) отверстие в плитке коронкой по той же привязке, плитку не сдвигать.
5. За приборами и в коробе (В1-6, К1-6, К1-4) — штриховым кольцом.
6. Гидроизоляция: 200 мм от ЧП по периметру; над ванной — до 2000 и 300 мм за борт (СП 29.13330.2011, п. 7.2 — на высоту замачивания); углы — лентой; акт скрытых работ, пролив.


	Лист	№ док.	Подпись	Дата
Дизайнер	Кырлан А.С.			14.11.26
Проверил				
Н. контр.				
Утв.				

Проект: Квартира 65 м² — **М 1:25**

Раскладка плитки. Ванная. Развёртки стен

Стадия	Лист	Листов
П	37	105

выпуск 14.11.2026 № 3aed0ef730 · стр. 37 из 105

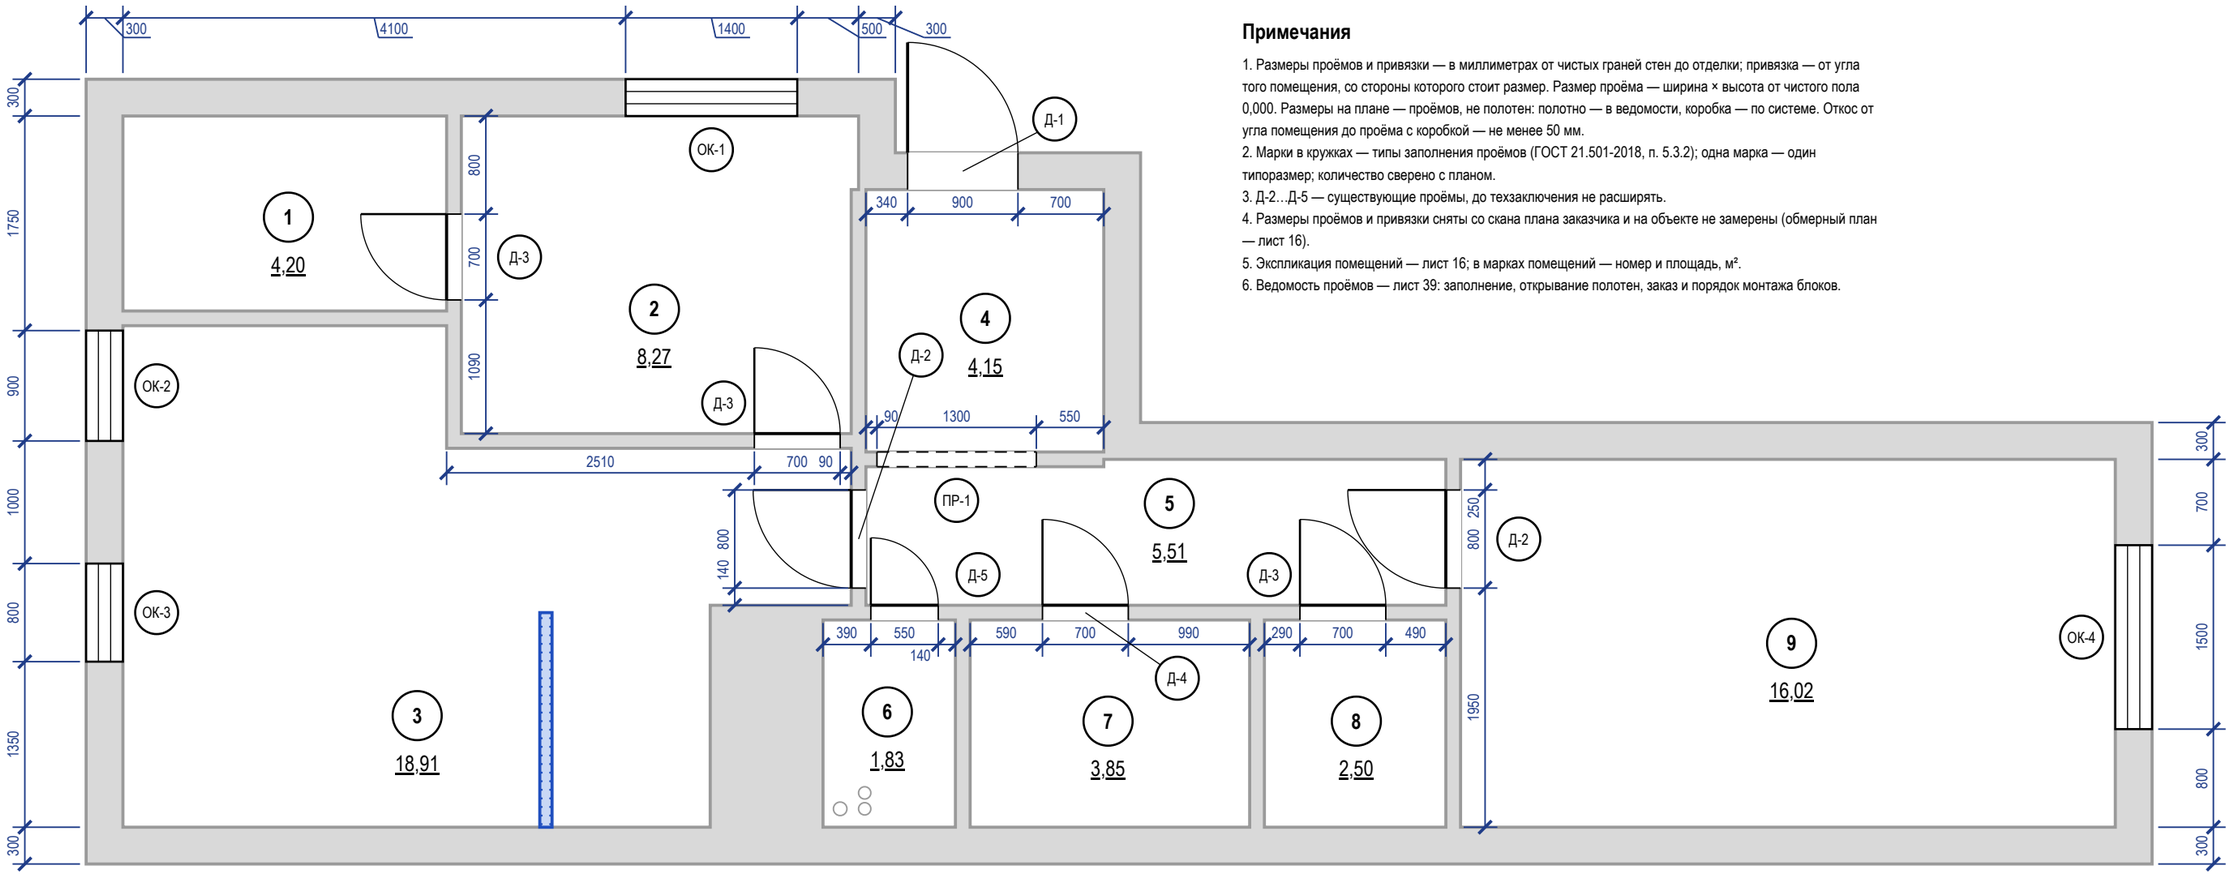

Примечания


1. Размеры проёмов и привязки — в миллиметрах от чистых граней стен до отделки; привязка — от угла того помещения, со стороны которого стоит размер. Размер проёма — ширина × высота от чистого пола 0,000. Размеры на плане — проёмов, не полотен: полотно — в ведомости, коробка — по системе. Откос от угла помещения до проёма с коробкой — не менее 50 мм.
2. Марки в кружках — типы заполнения проёмов (ГОСТ 21.501-2018, п. 5.3.2); одна марка — один типоразмер; количество сверено с планом.
3. Д-2…Д-5 — существующие проёмы, до техзаключения не расширять.
4. Размеры проёмов и привязки сняты со скана плана заказчика и на объекте не замерены (обмерный план — лист 16).
5. Экспликация помещений — лист 16; в марках помещений — номер и площадь, м².
6. Ведомость проёмов — лист 39: заполнение, открывание полотен, заказ и порядок монтажа блоков.

	Лист	№ док.	Подпись	Дата	Проект: Квартира 65 м²			М 1:50
Дизайнер	Кырлан А.С.			14.11.26	План размещения дверей	Стадия	Лист	Листов
Проверил						П	38	105
Н. контр.								
Утв.								


Ведомость заполнения проёмов

Марка	Наименование, обозначение	Проём ш×в, мм	Полотно (расч.)	Кол.	Откр.	Отделка полотна	Фурнитура	Прим.
Д-1	Блок дверной входной, ГОСТ 31173-2016	900×2100	блок задать	1	П	в комплекте блока	в комплекте блока (замки, глазок)	наружу
Д-2	Дверь скрытого монтажа, Profil Doors Invisible	800×2100	700×2050	2	Л, Л	S 1002-Y50R — пом. 3, S 1502-Y50R — пом. 5; S 1502-Y50R — пом. 5, No. 241 — пом. 9	скрытые петли 3D, магнитный замок	
Д-3	Дверь скрытого монтажа, Profil Doors Invisible	700×2100	600×2050	3	Л, П, П	V503 — пом. 1, S 1502-Y50R — пом. 2; S 1502-Y50R — пом. 2, S 1002-Y50R — пом. 3; S 1502-Y50R — пом. 5, S 0502-Y — пом. 8	скрытые петли 3D, магнитный замок	
Д-4	Дверь скрытого монтажа, Profil Doors Invisible	700×2100	600×2050	1	П	S 1502-Y50R — пом. 5, в тон облицовки — пом. 7	скрытые петли 3D, магнитный замок, фиксатор WC	порог 15
Д-5	Дверь скрытого монтажа, Profil Doors Invisible	550×2100	450×2050	1	П	S 1502-Y50R — пом. 5, в тон облицовки — пом. 6	скрытые петли 3D, магнитный замок, фиксатор WC	порог 15
ПР-1	Портал без заполнения	1300×2100		1				б/п
ОК-1	Блок оконный, ГОСТ 23166-2021	1400×1600		1				низ 800
ОК-2	Блок оконный, ГОСТ 23166-2021	900×1600		1				низ 800
ОК-3	Блок оконный, ГОСТ 23166-2021	800×1600		1				низ 800
ОК-4	Блок оконный, ГОСТ 23166-2021	1500×1600		1				низ 800


Схемы дверных блоков (1:25) — вид со стороны открывания; вершина треугольника — сторона петель

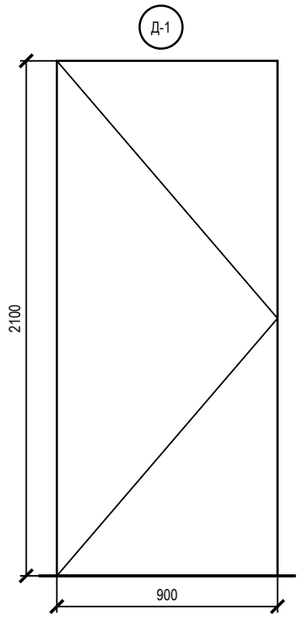


блок — по ГОСТ 31173
откр. П

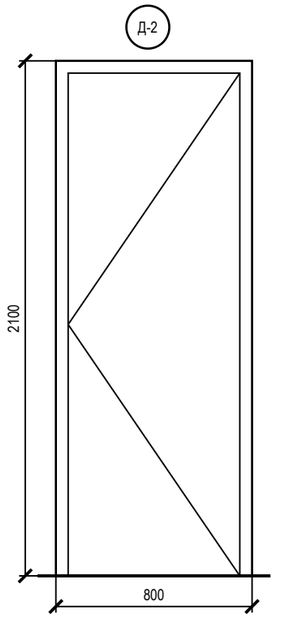


полотно 700×2050 (расч.)
откр. Л, Л

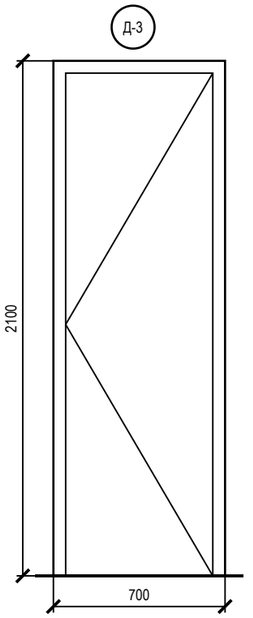


полотно 600×2050 (расч.)
откр. Л, П, П (схема — Л, остальные по плану)

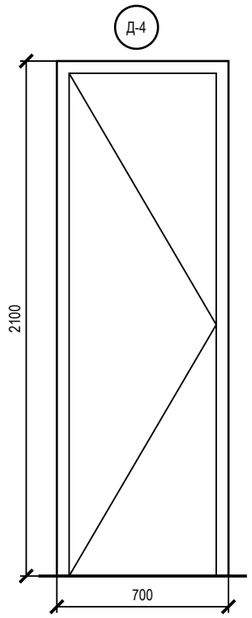

полотно 600×2050 (расч.)
откр. П

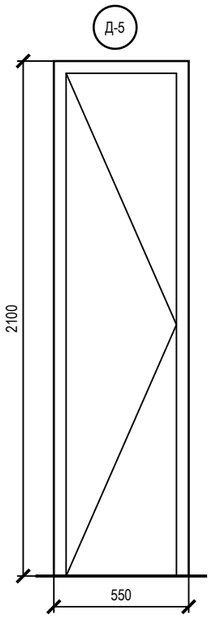

полотно 450×2050 (расч.)
откр. П

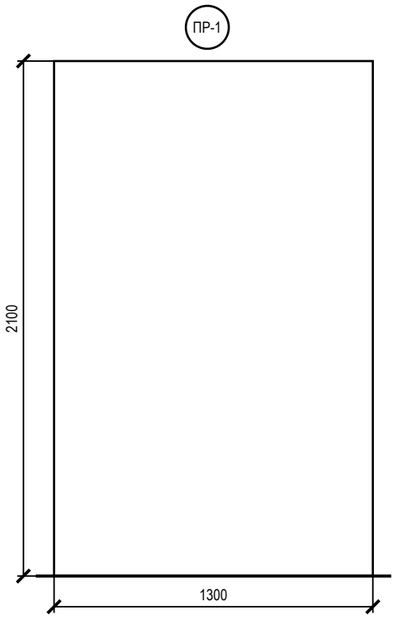


без заполнения

Примечания

1. Марки проёмов — те же, что на плане размещения дверей (лист 38); привязки проёмов — там же.
2. Открывание: Л — петли слева, П — справа, если смотреть со стороны, куда открывается полотно (на себя).
3. Скрытые двери (Д-2…Д-5): проём замерить в чистоте; блок заказать до штукатурки (≈ 30 дн.), короб ставить до штукатурки; полотно навесить после чистовой отделки, красить в цвет стен. Порядок — практика монтажа, изготовитель подтверждает.
4. Полотно «расч.» — по проёму и ряду изделия с запасом по каталогам, заказ — по таблице проёмов модели; Д-1: входной блок по ГОСТ 31173-2016 — задать при выборе блока.

	Лист	№ док.	Подпись	Дата	Проект: Квартира 65 м²			
Дизайнер	Кырлан А.С.			14.11.26	Ведомость заполнения проёмов	Стадия	Лист	Листов
Проверил						П	39	105
Н. контр.								
Утв.								

выпуск 14.11.2026 № 3aed0ef730 · стр. 39 из 105

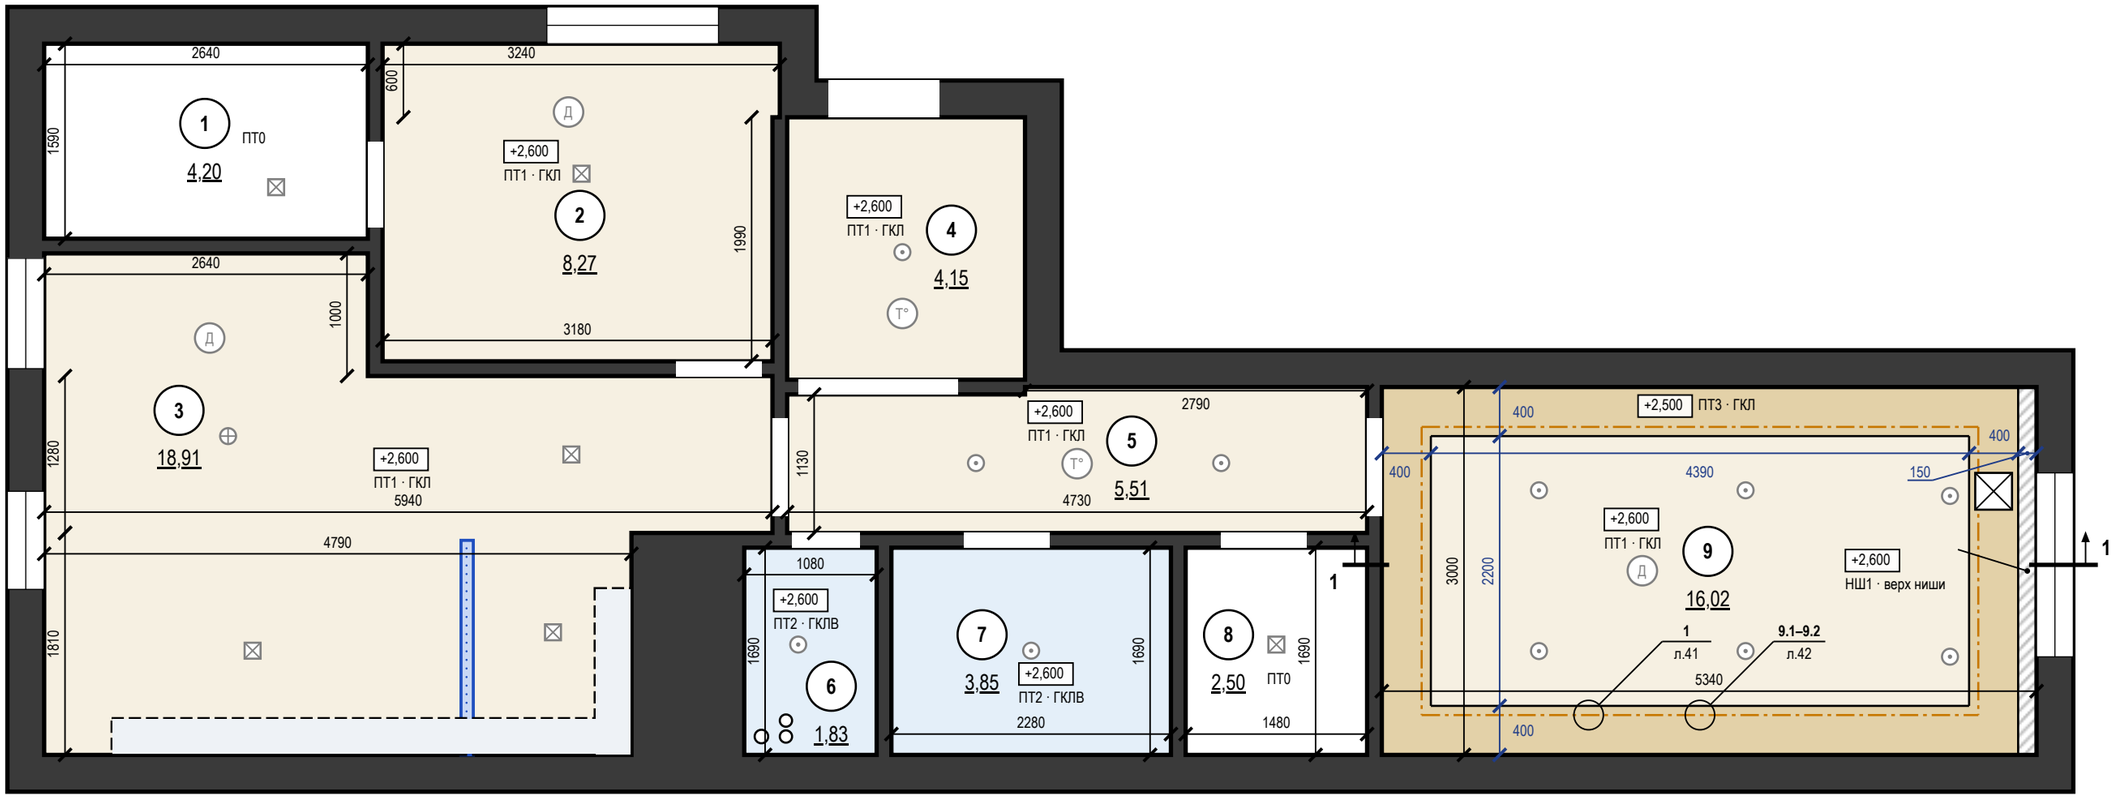

Ведомость потолков

Пом.	Марка	Конструкция	Низ / верх ниши	S, м²	Q
1, 8	ПТ0	Существующий потолок, окраска	+2,700	6,70	
2	ПТ1	ГКЛ П113	+2,600	8,27	Q3
3	ПТ1	То же	+2,600	18,91	Q3
4	ПТ1	То же	+2,600	4,15	Q3
5	ПТ1	То же	+2,600	5,51	Q3
6	ПТ2	ГКЛВ П113	+2,600	1,83	Q3
7	ПТ2	То же	+2,600	3,85	Q3
9	ПТ3	ГКЛ П113, короб LED	+2,500	5,91	Q3
9	ПТ1	ГКЛ П113	+2,600	9,66	Q3
9	НШ1	ниша под шторы 150×100	+2,600	0,45	
		Итого		**65,24**	

Ведомость вырезов и закладных в потолке

Марка	Устройство	Кол.	Пом.
	Светильник встраиваемый (марки — план освещения)	11	4, 5, 6, 7, 9
	Светильник накладной (марки — план освещения)	6	1, 2, 3, 8
	Светильник подвесной (марки — план освещения)	1	3
ИП2	Извещатель дымовой	3	2, 3, 9
ИП3, ИП4	Извещатель тепловой	2	4, 5
	Люк ревизии 300×300	1	9


Примечания

1. За отметку ±0,000 принят уровень чистого пола сухих помещений (готовое покрытие), а не существующего пола; пол пом. 6, 7 — −0,015; верх плиты перекрытия −0,064 — расчётный по пирогу пола, не замерен; существующий пол снимается до плиты, его отметка не замерена. Отметки в прямоугольниках — низ потолка; низ перекрытия +2,700. Марка потолка — одна конструкция и отметка на весь альбом.
2. Размеры помещений в свету (ширина × длина, мм), не поместившиеся на плане: пом. 4 — 1940 × 2140.
3. Потолки ГКЛ — каркасная система П113: подвесы через 1000 (с запасом: СП 163, табл. 14 — до 1100 при 0,15 кН/м²), несущие профили через 500, основные через 1200 мм; листы — поперёк несущих профилей. В помещениях 6, 7 — ГКЛВ на оцинкованном каркасе.
4. Нижний уровень — пояс-короб по периметру шириной 400 мм, верхний — поле внутри пояса: пом. 9.
5. LED-лента в алюминиевом профиле посередине карниза короба шириной 400 мм (узел 1, лист 41); длина по плану: пом. 9 — 13,8 м (в плане освещения 13,8).
6. Ниши под шторы 150×100 мм — на всю длину стены с окном; карниз — на закладной до обшивки (узел 2, лист 41).
7. Примыкание к стенам: теневой шов 15 мм, техзазор 3 мм — пом. 2, 3, 4, 5, 9, по стенам, выровненным штукатуркой (узел 1); пом. 6, 7 — разделительная лента.
8. Светильники и потолочные устройства — подложка с планов освещения, слаботочных систем и вентиляции (положение — по ним); вырезы и закладные — по ведомости на листе, до обшивки; отверстия не совмещать с профилями, глубина корпуса светильника до 70 мм.
9. Разрезы 1–1 — на листе 41; высоты мебели и дверных блоков сверены с низом потолка в разрезах.
10. Шпаклевание ГКЛ и условия приёмки — Q3: рассеянный дневной свет, осмотр с 2 м; боковой свет не оценивается.
11. Пом. 3: короб воздуховода кухонной вытяжки ГКЛ 300×200 мм (ширина от стены × высота), низ +2,500, длина 5,00 м — по трассе плана вентиляции, вдоль стен до входа в канал под воздуховод Ø125; каркас ПН 28×27 по стене и плите, ПП 60×27, лист ГКЛ 12,5.
12. Люки ревизии 300×300 мм — по центру блоков питания LED (БП3; координаты — план освещения).
13. ПТ0 — пом. 1, 8: существующий потолок, окраска, без подвесного потолка, низ +2,700; материал и цвет — по ведомости отделки.

	Лист	№ док.	Подпись	Дата	Проект: Квартира 65 м²			М 1:50
Дизайнер	Кырлан А.С.			14.11.26	План потолков	Стадия	Лист	Листов
Проверил						П	40	105
Н. контр.								
Утв.								


Разрез 1–1 (М 1:40)

Пом. 9 Детская; линия разреза — план потолков, лист 40

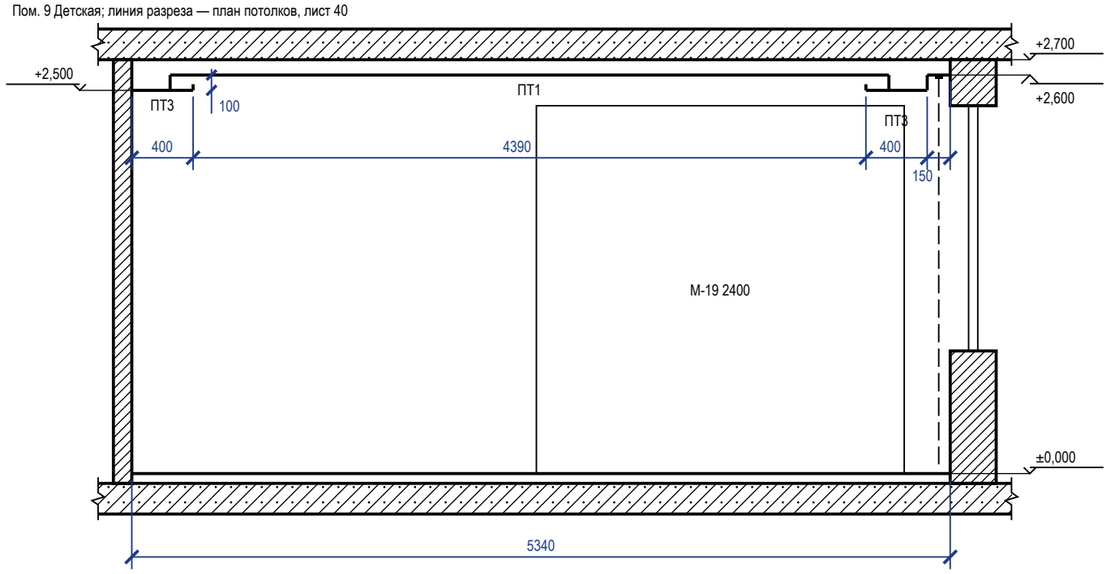

1 Короб с LED-подсветкой, теневой шов (М 1:10)


Пом. 9; карниз 150×100, щель под свет 60 мм

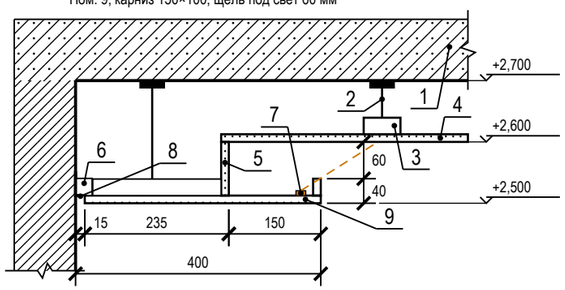

1 — плита перекрытия
2 — подвес прямой, шаг 1000 мм
3 — ПП 60×27: несущие через 500, основные через 1200 мм
4 — ГКЛ 12,5 по П113 — верхний уровень
5 — задняя стенка и бортик карниза — ГКЛ 12,5
6 — ПН 28×27 по периметру, к стене через 500 мм
7 — LED-лента в алюминиевом профиле
8 — теневой профиль: шов 15 мм, зазор 3 мм
9 — низ короба — ГКЛ 12,5 по ПП 60×27

2 Ниша под шторы (М 1:10)

Пом. 9; без подсветки; закладные под карниз — до обшивки

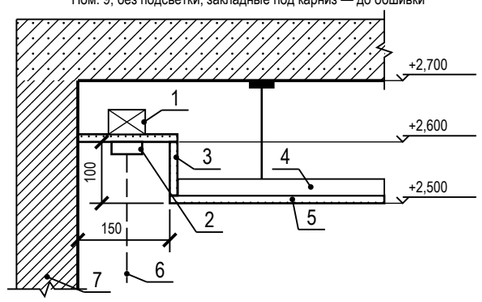

1 — закладная под карниз — брус 40×50
2 — карниз (шина), высота с верхом портьеры 80 мм
3 — стенка и потолок ниши — ГКЛ 12,5
4 — ПП 60×27 — каркас короба
5 — низ короба нижнего уровня — ГКЛ 12,5
6 — портьера
7 — стена с окном

Условные обозначения

- плита перекрытия в сечении
- стена в сечении
- потолок ГКЛ в сечении; под линией — марка потолка (план потолков)
- мебель и дверные проёмы за секущей плоскостью; число — марка и верх от чистого пола, мм
- портьера в нише под шторы

Примечания


1. Разрезы — по линиям 1–1 на плане потолков (лист 40). Отметки — от ±0,000 чистого пола, м; размеры — мм.
2. Высоты мебели и дверных блоков за секущей плоскостью сверены с низом потолка над ними: верх ниже низа короба и поля.
3. ГКЛ 12,5 мм по каркасу П113; перепад уровней и бортик карниза — ГКЛ по ПП 60×27 (узел 1 — на этом листе). Ниша под шторы — на всю длину стены с окном, карниз на закладной до обшивки (узел 2 — на этом листе).
4. Толщины плит перекрытия и пирога пола показаны условно.
5. Сечения потолков по помещениям М 1:10 (отметки помещения, профили, подвесы, крепёж, изделия) — лист 42.
6. Ведомость объёмов потолков (лист ГКЛ, профиль, подвесы, лента, блоки питания, люки) — на листе 42.

	Лист	№ док.	Подпись	Дата	Проект: Квартира 65 м²			М 1:40; 1:10
Дизайнер	Кырлан А.С.			14.11.26	Разрезы и узлы потолков	Стадия	Лист	Листов
Проверил						П	41	105
Н. контр.								
Утв.								

выпуск 14.11.2026 № 3aed0ef730 · стр. 41 из 105

Сечение 9.1. Короб с LED-подсветкой, теневой шов (М 1:10)


Пом. 9 Детская; карниз 150×100, щель под свет 60 мм

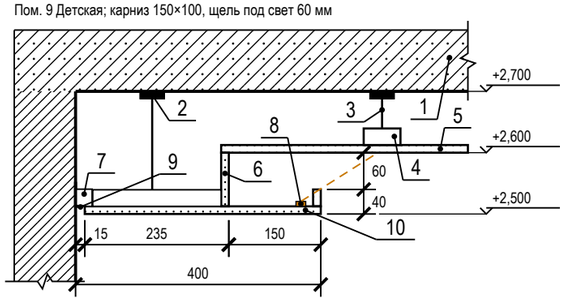

1 — плита перекрытия
2 — анкер-клин к плите — по одному на подвес
3 — подвес прямой, шаг 1000 мм
4 — ПП 60×27: несущие через 500, основные через 1200 мм; соединители одноуровневые, шурупы LN 3,5×9
5 — ГКЛ 12,5 по П113 — верхний уровень; шурупы TN 3,5×25 через 170 мм
6 — задняя стенка и бортик карниза — ГКЛ 12,5
7 — ПН 28×27 по периметру — дюбель-гвоздь через ≤ 500 мм, не менее 3 на профиль
8 — LED-лента 9,6 Вт/м, 24 В в алюминиевом профиле
9 — теневой профиль: шов 15 мм, зазор 3 мм
10 — низ короба — ГКЛ 12,5 по ПП 60×27

Сечение 9.2. Ниша под шторы (М 1:10)

Пом. 9 Детская; без подсветки; закладные под карниз — до обшивки

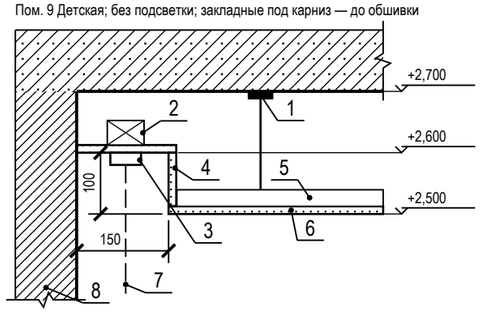

1 — анкер-клин к плите — по одному на подвес; подвес прямой, шаг 1000 мм
2 — закладная под карниз — брус 40×50
3 — карниз (шина), высота с верхом портьеры 80 мм
4 — стенка и потолок ниши — ГКЛ 12,5
5 — ПП 60×27 — каркас короба, основные через 1200 мм; соединители одноуровневые, шурупы LN 3,5×9
6 — низ короба нижнего уровня — ГКЛ 12,5; шурупы TN 3,5×25 через 170 мм
7 — портьера
8 — стена с окном

Ведомость объёмов потолков

Позиция	Ед.	Кол.	Пом.
Лист ГКЛ 12,5	м²	57,10	2, 3, 4, 5, 9
Лист ГКЛВ 12,5	м²	5,68	6, 7
Борта и карнизы (входят в площади листов выше)	м²	4,24	9
Профиль ПП 60×27	м	169,79	2, 3, 4, 5, 6, 7, 9
Профиль ПН 28×27	м	128,02	2, 3, 4, 5, 6, 7, 9
Подвес прямой	шт.	64	2, 3, 4, 5, 6, 7, 9
Анкер-клин к плите	шт.	64	2, 3, 4, 5, 6, 7, 9
Шуруп TN 3,5×25	шт.	1444	2, 3, 4, 5, 6, 7, 9
Лента армирующая для швов	м	75,34	2, 3, 4, 5, 6, 7, 9

Ведомость объёмов потолков (окончание)

Позиция	Ед.	Кол.	Пом.
Шпаклёвка для швов	кг	25,11	2, 3, 4, 5, 6, 7, 9
Грунтовка (швы)	л	6,28	2, 3, 4, 5, 6, 7, 9
Лента разделительная по периметру	м	81,88	2, 3, 4, 5, 6, 7, 9
Сплошная шпаклёвка и окраска (площадь развёртки)	м²	62,78	2, 3, 4, 5, 6, 7, 9
Лента LED	м	13,78	9
Требуемая мощность блоков питания	Вт	172	9
Установленная мощность блоков питания	Вт	200	9
Блок питания LED	шт.	1	9
Люк ревизии	шт.	1	9

Условные обозначения


— · — LED-лента в нише подсветки (карниз короба, ниша фигуры)

Примечания

1. Сечения потолков М 1:10 по помещениям с нишами LED и нишами под шторы: отметки и размеры этого помещения от ±0,000 чистого пола (м, мм). Положение — по плану потолков (лист 40): короб и ниша LED — по линиям ленты, ниша под шторы — у стены с окном; типовые узлы по группам помещений — на листе 41.
2. Крепёж: подвес прямой к плите на анкер-клине — по одному на подвес (Knauf П113); ПН к стенам — дюбель-гвоздь через ≤ 500 мм, не менее 3 на профиль (серия 1.045.9-2.08); лист 12,5 — шурупы TN 3,5×25 через 170 мм (СП 163, табл. 15); профили между собой — соединители одноуровневые, шурупы LN 3,5×9.
3. Изделие карниза, профиля LED и галтели подписано артикулом из данных; где артикул не выбран, сечение дано по габаритам из данных (ширина и глубина ниши, щель под свет), изделие подбирается по ним.
4. Ведомость объёмов — по геометрии плана потолков: Лист ГКЛ 12,5 — плоскости уровней + борта (без арочных участков); Лист ГКЛВ 12,5 — плоскости уровней + борта; Борта и карнизы — длина перепада × перепад; Профиль ПП 60×27 — S × (1/шаг несущ. + 1/шаг осн.) + стойки бортов; Профиль ПН 28×27 — периметр стен + 2 × перепады + карнизы; Подвес прямой — по раскладке: S уровня / (шаг осн. × шаг подвесов), пояс уже шага — ряд вдоль пояса, фигура — по контуру; шаг подвесов — не больше табл. 14 СП 163; Анкер-клин к плите — по одному на подвес (Knauf П113); Шуруп TN 3,5×25 — 23 шт./м² (Knauf П113, табл. 2 альбома П 11); Лента армирующая для швов — 1,2 м/м² листа (Knauf); Шпаклёвка для швов — 0,4 кг/м² листа, только швы (Knauf); Грунтовка (швы) — 0,1 л/м² листа, только швы (Knauf); Лента разделительная по периметру — периметр стен под потолком ГКЛ; Сплошная шпаклёвка и окраска (площадь развёртки) — плоскости + борта; расход — по паспорту материала (норма расхода на сплошной слой не подтверждена); Лента LED — по оси карниза и ниши фигуры (план потолков); Требуемая мощность блоков питания — Вт/м × длина × 1,3; Установленная мощность блоков питания — сумма мощностей блоков по плану освещения; Блок питания LED — блоки потолочных лент по плану освещения (БП3); Люк ревизии — план потолков; без запаса на подрезку (при закупке листа: ×1,075 при S > 20 м², ×1,175 — 10–20 м², ×1,275 — < 10 м²).

	Лист	№ док.	Подпись	Дата	Проект: Квартира 65 м²			М 1:10
Дизайнер	Кырлан А.С.			14.11.26	Сечения потолков М 1:10	Стадия	Лист	Листов
Проверил						П	42	105
Н. контр.								
Утв.								

выпуск 14.11.2026 № 3aed0ef730 · стр. 42 из 105

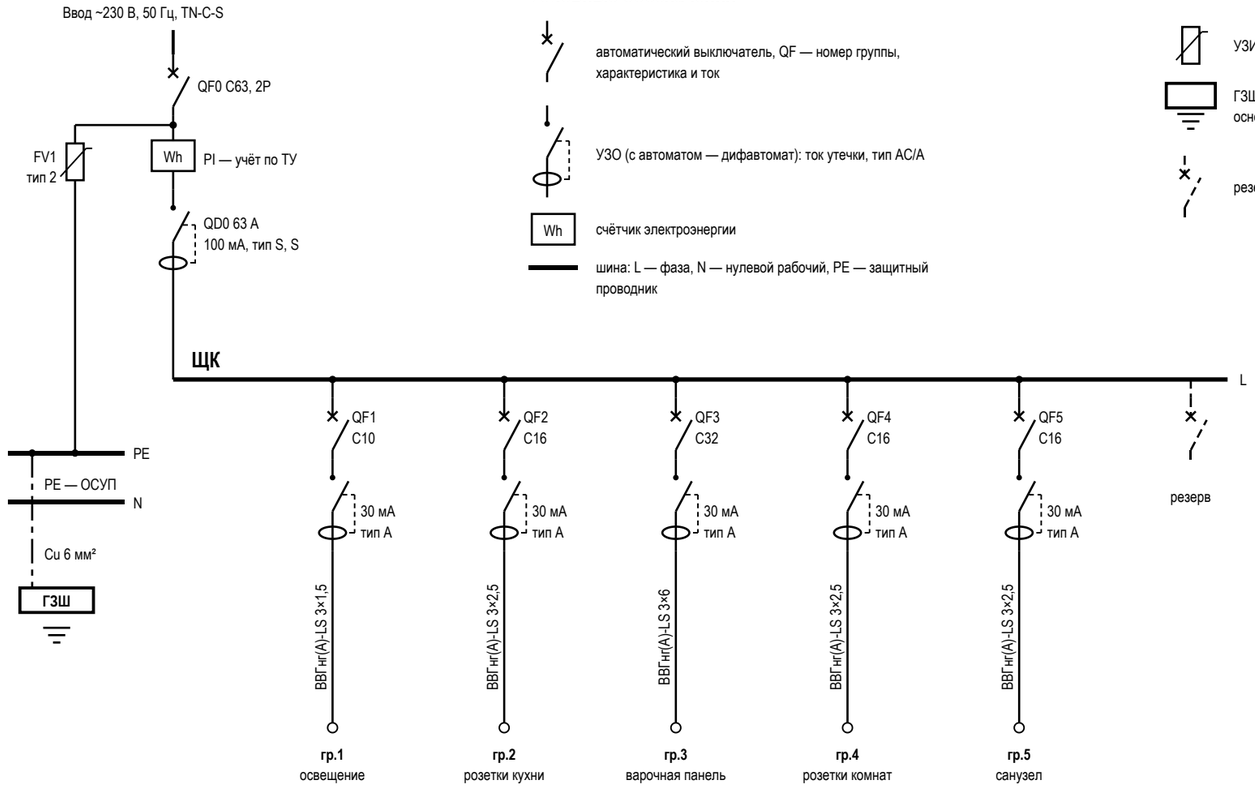

Условные обозначения

автоматический выключатель, QF — номер группы, характеристика и ток

УЗО (с автоматом — дифавтомат): ток утечки, тип AC/A

Wh — счётчик электроэнергии

шина: L — фаза, N — нулевой рабочий, PE — защитный проводник

УЗИП (ограничитель перенапряжений), FV — марка

ГЗШ — главная заземляющая шина; штрихпунктир — проводник основной системы уравнивания потенциалов (ОСУП)

резервный аппарат (не менее 20 % групп)

Данные щитка

Показатель	Значение
Номер щитка	ЩК
Тип	ЩРВ-П-24, IP41
Уст. мощность, кВт	
Разреш. мощность, кВт	15
Расчётная, кВт	9,8
Автоматы 1п: занят. / рез.	5 / 1
Модулей: всего / занято	24 / 16
Ток на вводе, А	63
Вводной аппарат	QF0 C63, 2P
УЗИП	FV1, тип 2, ЩК, после счётчика
ГЗШ, проводник ОСУП	Cu 6 мм²

Таблица групп щита ЩК и кабельный журнал

№	Назначение	Помещения	Автомат	УЗО / дифавтомат	Кабель	Длина, м	Р, кВт	Точек
1	освещение	1, 2, 3, 4, 5, 6, 7, 8, 9	C10	30 мА, тип A	ВВГнг(A)-LS 3×1,5	140,7		38
2	розетки кухни	3	C16	30 мА, тип A	ВВГнг(A)-LS 3×2,5	20,4		3
3	варочная панель	3	C32	30 мА, тип A	ВВГнг(A)-LS 3×6	17,2		1
4	розетки комнат	2, 3, 5	C16	30 мА, тип A	ВВГнг(A)-LS 3×2,5	52,4		10
5	санузел	7, 9	C16	30 мА, тип A	ВВГнг(A)-LS 3×2,5	47,1		9
	Итого по сечениям ВВГнг(A)-LS, м: 3×1,5 — 140,7; 3×2,5 — 119,9; 3×6 — 17,2					277,8		

Примечания

1. Схема однолинейная: одна линия — фаза, N и PE группы; аппараты — в отключённом положении (ГОСТ 2.702, ГОСТ 2.755). Номера групп — как у точек на планах (гр.). За отметку 0,000 принят уровень чистого пола; высота щита — по плану розеток.
2. Розеточные и мокрые линии — через УЗО или дифавтомат с током утечки не более 30 мА (ПУЭ 7.1.79); в санузле выполнить ДСУП (ПУЭ 7.1.87–7.1.88).
3. УЗО тип A — для линий с электроникой, стиральной и посудомоечной машиной, LED-драйверами; тип AC — только для чисто активной нагрузки.
4. Кабель — медный, исполнение нг(A)-LS (ГОСТ 31565-2012); скрытая прокладка только горизонтально и вертикально, фактические трассы зафиксировать исполнительной схемой до закрытия отделкой.
5. Номинал автомата — не выше допустимого тока кабеля: 1,5 мм² — до 10 А, 2,5 мм² — до 16 А. Резерв щита — не менее 20 % модулей.
6. Расчёт нагрузок, токов КЗ, селективности и сечений — по проекту ЭОМ организации с допуском СРО; лист задаёт состав, расположение и группы.
7. УЗИП FV1 — после вводного автомата, проводник к шине PE — кратчайший, без петель. Шина PE щита соединяется с ГЗШ проводником ОСУП; к ГЗШ присоединяются трубы водопровода и отопления на вводе в квартиру (ПУЭ 7.1.87). Шины N и PE — раздельные, после разделения PEN не объединяются.
8. До подключения нагрузки — приёмо-сдаточные испытания с протоколом: сопротивление изоляции линий не менее 0,5 МОм, срабатывание УЗО по току и времени, непрерывность защитных проводников PE (ПУЭ, гл. 1.8).

	Лист	№ док.	Подпись	Дата	Проект: Квартира 65 м²			
Дизайнер	Кырлан А.С.			14.11.26	Однолинейная схема щита	Стадия	Лист	Листов
Проверил						П	43	105
Н. контр.								
Утв.								

Группы щита ЩК (1)

№	Назначение	Руст, кВт	Кс	Ррасч, кВт	Iрасч, А	Автомат	Кабель
1	освещение	0	0,6	0	0	C10	3×1,5
2	розетки кухни	0	0,4	0	0	C16	3×2,5
3	варочная панель	0	0,6	0	0	C32	3×6

Группы щита ЩК (2)

№	Назначение	Руст, кВт	Кс	Ррасч, кВт	Iрасч, А	Автомат	Кабель
4	розетки комнат	0	0,4	0	0	C16	3×2,5
5	санузел	0	0,7	0	0	C16	3×2,5

Итог по квартире

Показатель	Значение
Установленная мощность Σ Руст	0 кВт
Σ Руст × Кс по группам	0 кВт
Коэффициент одновременности	0,7
Расчётная мощность квартиры Ррасч	0 кВт
Расчётный ток Iрасч (230 В, cosφ 0,95)	0 А
Разрешённая мощность	15 кВт
Запас до разрешённой	100 %
Вводной аппарат	C63, 2P


Примечания

1. Руст — установленная мощность группы по данным щита (приборы — по паспорту, розетки общего назначения — оценка 0,1 кВт на гнездо). Кс — коэффициенты спроса: освещение 0,6; розетки 0,4; варочная и духовой 0,6; кондиционеры 0,8; тёплый пол 1,0; прочие 0,7; одновременность 0,7.
2. Коэффициенты — ориентир исполнителя, не табличные значения нормы; расчёт нагрузки подтверждает инженер ЭОМ (СП 256.1325800.2016). Под разрешённую мощность они не подгоняются.
3. Вывод: запас 100 % (расчётная 0 кВт при разрешённой 15 кВт).
4. Розеточные и мокрые линии — через УЗО или дифавтомат с током утечки не более 30 мА (ПУЭ 7.1.79); в санузле выполнить ДСУП (ПУЭ 7.1.87–7.1.88).

	Лист	№ док.	Подпись	Дата	Проект: Квартира 65 м²			
Дизайнер	Кырлан А.С.			14.11.26	Таблица нагрузок щита	Стадия	Лист	Листов
Проверил						П	44	105
Н. контр.								
Утв.								

выпуск 14.11.2026 № 3aed0ef730 · стр. 44 из 105

План принципиальных трасс (М 1:100)

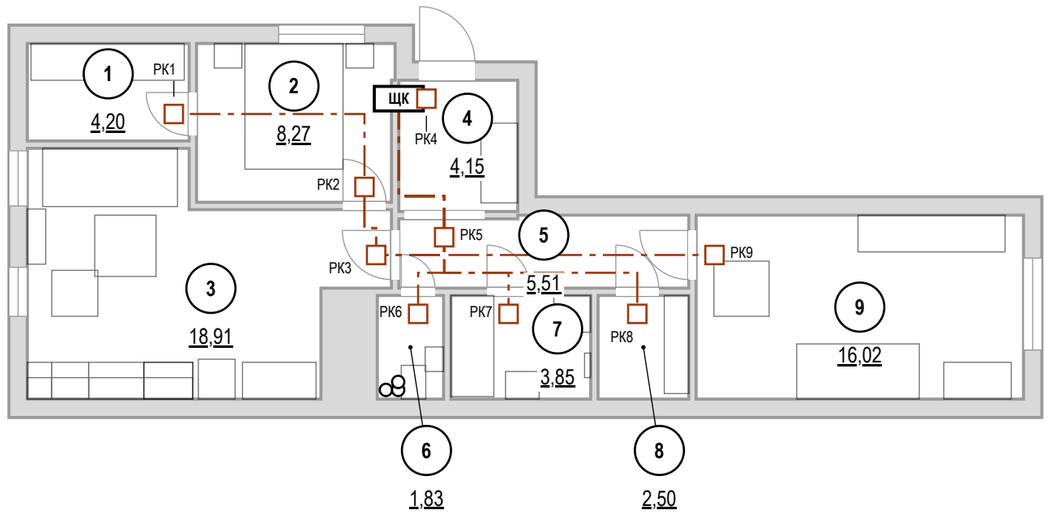

Кабель по группам ВВГнг(А)-LS, м

Гр.	мм²	Трасса	Данные
1	3×1,5	140,7	
2	3×2,5	20,4	
3	3×6	17,2	

Гр.	мм²	Трасса	Данные
4	3×2,5	52,4	
5	3×2,5	47,1	
Σ		**277,8**	

Экспликация помещений

№	Помещение	Площадь, м²
1	Гардеробная	4,20
2	Спальня	8,27
3	Кухня-гостиная	18,91
4	Прихожая	4,15
5	Коридор	5,51
6	Санузел	1,83
7	Ванная	3,85
8	Кладовая	2,50
9	Детская	16,02
	Итого (общая площадь)	65,24

Объёмы прокладки

Работа, материал	Ед.	Кол.
Гофротруба Ø20 в потолочном пространстве	м	97,8
Кабель-канал плинтуса для силовых линий	м	83,3
Короб или накладной канал для вертикальных спусков и подъёмов	м	51
Коробка распределительная (РК) над дверью помещения	шт	9
Слаботочка: кабель домофона	м	3,1
Слаботочка: Кабель коаксиальный RG-6 (75 Ом) к розеткам ТВ	м	30,2
Слаботочка: Кабель U/UTP кат. 5е (LAN, Wi-Fi и камеры по PoE)	м	42,7
Слаботочка: U/UTP кат. 6 (LAN, Wi-Fi, камеры)	м	14,2
Слаботочка: гофротруба Ø20 отдельно от силовых	м	81,2

Штробы — только после заключения

Работа	Ед.	Кол.
Вертикальные штробы 20×20 мм от потолка до каждой настенной точки (в маршрут без штроб не входят)	м	69,81

Условные обозначения

- **ЩК** — щит квартирный
- РК — распределительная коробка над дверью помещения
- магистраль от щита к РК: потолочное пространство, гофра
- мебель и сантехприборы — подложка


Примечания

1. За отметку 0,000 принят уровень чистого пола. Высоты Н — от чистого пола до оси изделия; привязки — от чистовой грани стены до оси механизма (у рамки на несколько постов — до оси рамки).
2. Розеточные и мокрые линии — через УЗО или дифавтомат с током утечки не более 30 мА (ПУЭ 7.1.79); в санузле выполнить ДСУП (ПУЭ 7.1.87–7.1.88).
3. Кабель — медный, исполнение нг(А)-LS (ГОСТ 31565-2012); скрытая прокладка только горизонтально и вертикально, фактические трассы зафиксировать исполнительной схемой до закрытия отделкой.
4. Расчёт нагрузок, токов КЗ, селективности и сечений — по проекту ЭОМ организации с допуском СРО; лист задаёт состав, расположение и группы.
5. Длины — по плану: от щита вверх в потолочное пространство, по дверям и коридору без захода в мокрые помещения к распределительной коробке над дверью, далее к точкам; вертикали считаются вниз и обратно (у последней точки цепочки — в один конец); запас 10 %. Трассы принципиальные: фактическую зафиксировать исполнительной схемой до закрытия отделкой.
6. Несущие стены не определены: штробы в стенах не выполнять. Маршрут проложен без штроб: горизонтали — за потолком в гофре (97,8 м) и в кабель-канале плинтуса (83,3 м), вертикали — в коробе или накладном канале (89,7 м кабеля). Точек: за потолком — 21, спуск из потолка — 8, по плинтусу — 11, плинтус и подъём — 22.
7. Вариант со штробами — работа после технического заключения: 69,81 м вертикальных штроб от потолка до каждой настенной точки; условие — только после технического заключения: стена не несущая (или вертикальная штроба в несущей согласована конструктором), глубина и ширина 20–25 мм, не в зонах 0–2 ванной. Без заключения и согласования конструктора в смету и в график эта работа не входит.
8. Слаботочные сети: кабели и точки считаются по лучам от ЩС (лист слаботочных сетей): 90 м, портов патч-панели и коммутатора не менее 4. Изделия — в ведомости изделий.

	Лист	№ док.	Подпись	Дата	Проект: Квартира 65 м²			М 1:100
Дизайнер	Кырлан А.С.			14.11.26	План принципиальных трасс	Стадия	Лист	Листов
Проверил						П	45	105
Н. контр.								
Утв.								

выпуск 14.11.2026 № 3aed0ef730 · стр. 45 из 105

План розеток (М 1:50)

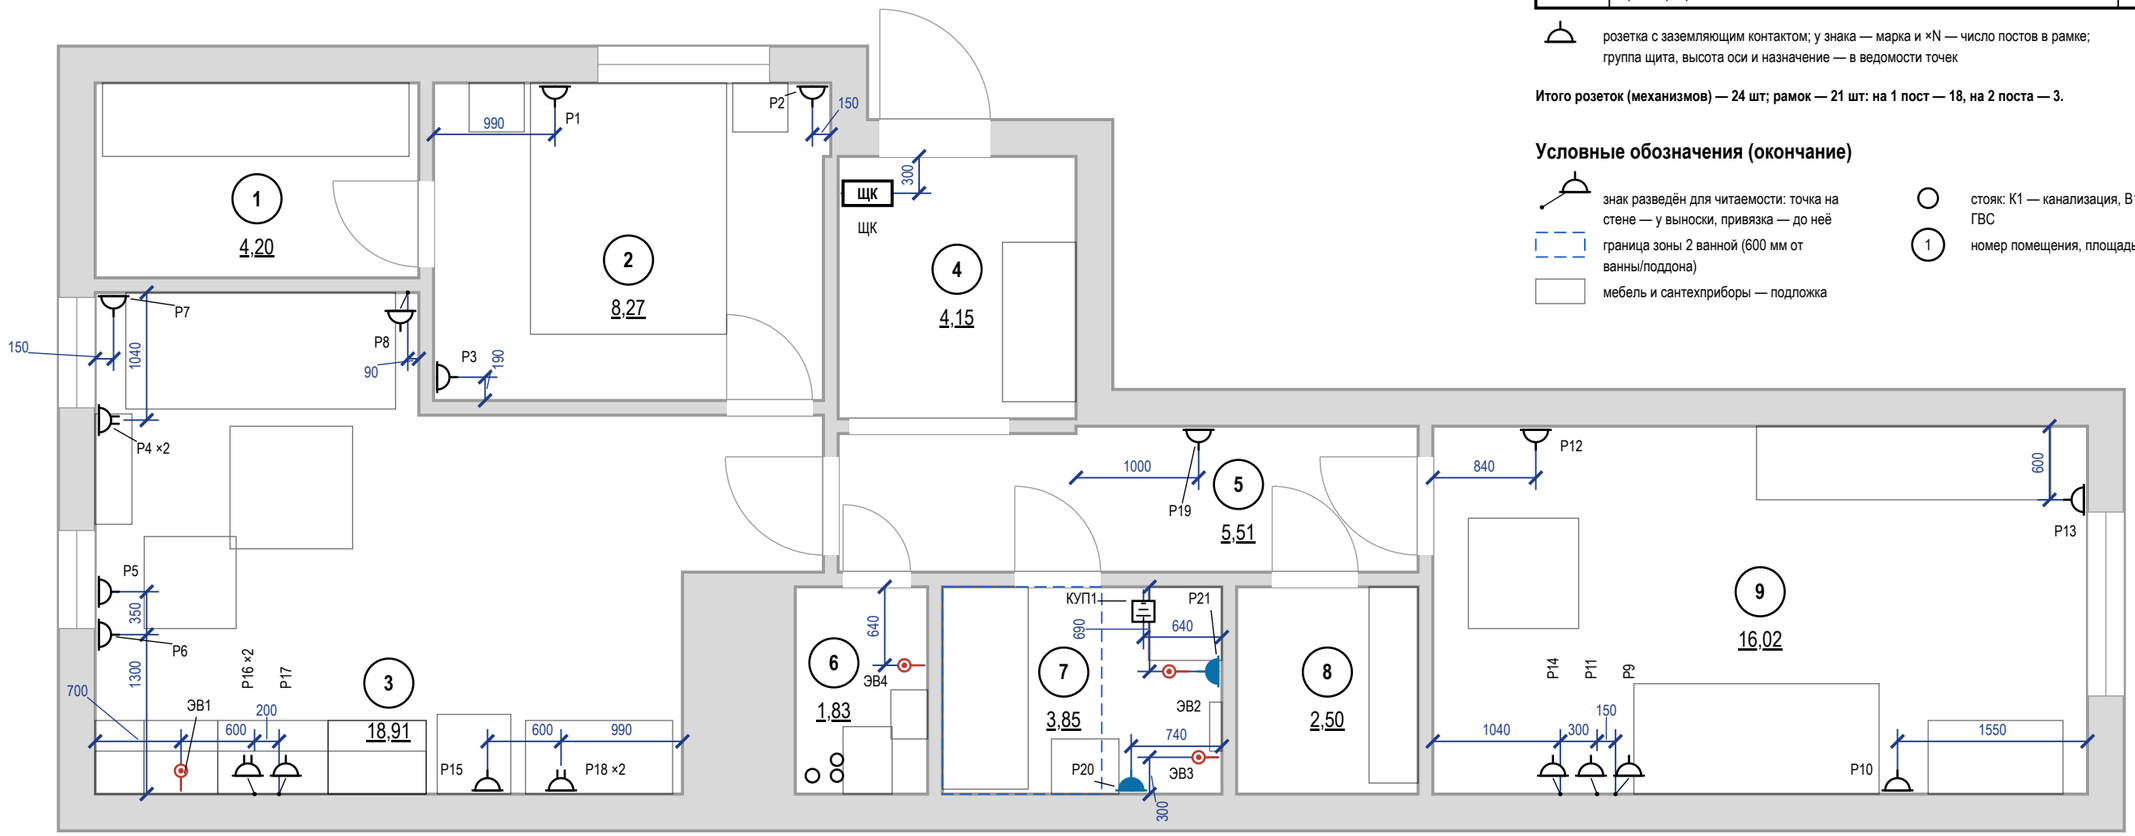

Условные обозначения

Знак	Тип изделия	H, мм	Кол., шт
	Розетка с заземлением	300	10
	То же	у знака	6
	Блок розеток с заземлением, рамка 2 поста	у знака	3
	Розетка с заземлением IP44	1100	2
	Вывод кабеля к прибору	у знака	4
	КУП (уравнивание потенциалов)	300	1
ЩК	Щит квартирный	1700	1

розетка с заземляющим контактом; у знака — марка и ×N — число постов в рамке; группа щита, высота оси и назначение — в ведомости точек

Итого розеток (механизмов) — 24 шт; рамок — 21 шт: на 1 пост — 18, на 2 поста — 3.

Условные обозначения (окончание)

знак разведён для читаемости: точка на стене — у выноски, привязка — до неё

граница зоны 2 ванной (600 мм от ванны/поддона)

мебель и сантехприборы — подложка

стояк: К1 — канализация, В1 — ХВС, Т3 ГВС


1 — номер помещения, площадь м²

Примечания

1. За отметку 0,000 принят уровень чистого пола. Высоты H — от чистого пола до оси изделия; привязки — от чистовой грани стены до оси механизма (у рамки на несколько постов — до оси рамки).
2. Высоты H и группы щита — в ведомости электроточек: розетки — 300 мм от чистого пола до оси механизма, если в ведомости не указано иное; выводы кабеля — по паспорту прибора.
3. Розетки в санузле — только вне зон 0–2 (ПУЭ 7.1.48, ГОСТ Р 50571.7.701-2024), IP44, через УЗО 30 мА.
4. Розеточные и мокрые линии — через УЗО или дифавтомат с током утечки не более 30 мА (ПУЭ 7.1.79); в санузле выполнить ДСУП (ПУЭ 7.1.87–7.1.88).
5. Кабель — медный, исполнение нг(A)-LS (ГОСТ 31565-2012); скрытая прокладка только горизонтально и вертикально, фактические трассы зафиксировать исполнительной схемой до закрытия отделкой.
6. Расчёт нагрузок, токов КЗ, селективности и сечений — по проекту ЭОМ организации с допуском СРО; лист задаёт состав, расположение и группы.
7. Выводы кухонной техники — после утверждения проекта кухни (ориентировочно); привязки выводов даны от осей модулей гарнитура и пересматриваются вместе с проектом кухни.

	Лист	№ док.	Подпись	Дата	Проект: Квартира 65 м²			М 1:50
Дизайнер	Кырлан А.С.			14.11.26	План розеток и электровыводов	Стадия	Лист	Листов
Проверил						П	46	105
Н. контр.								
Утв.								

План слаботочных сетей (М 1:50)

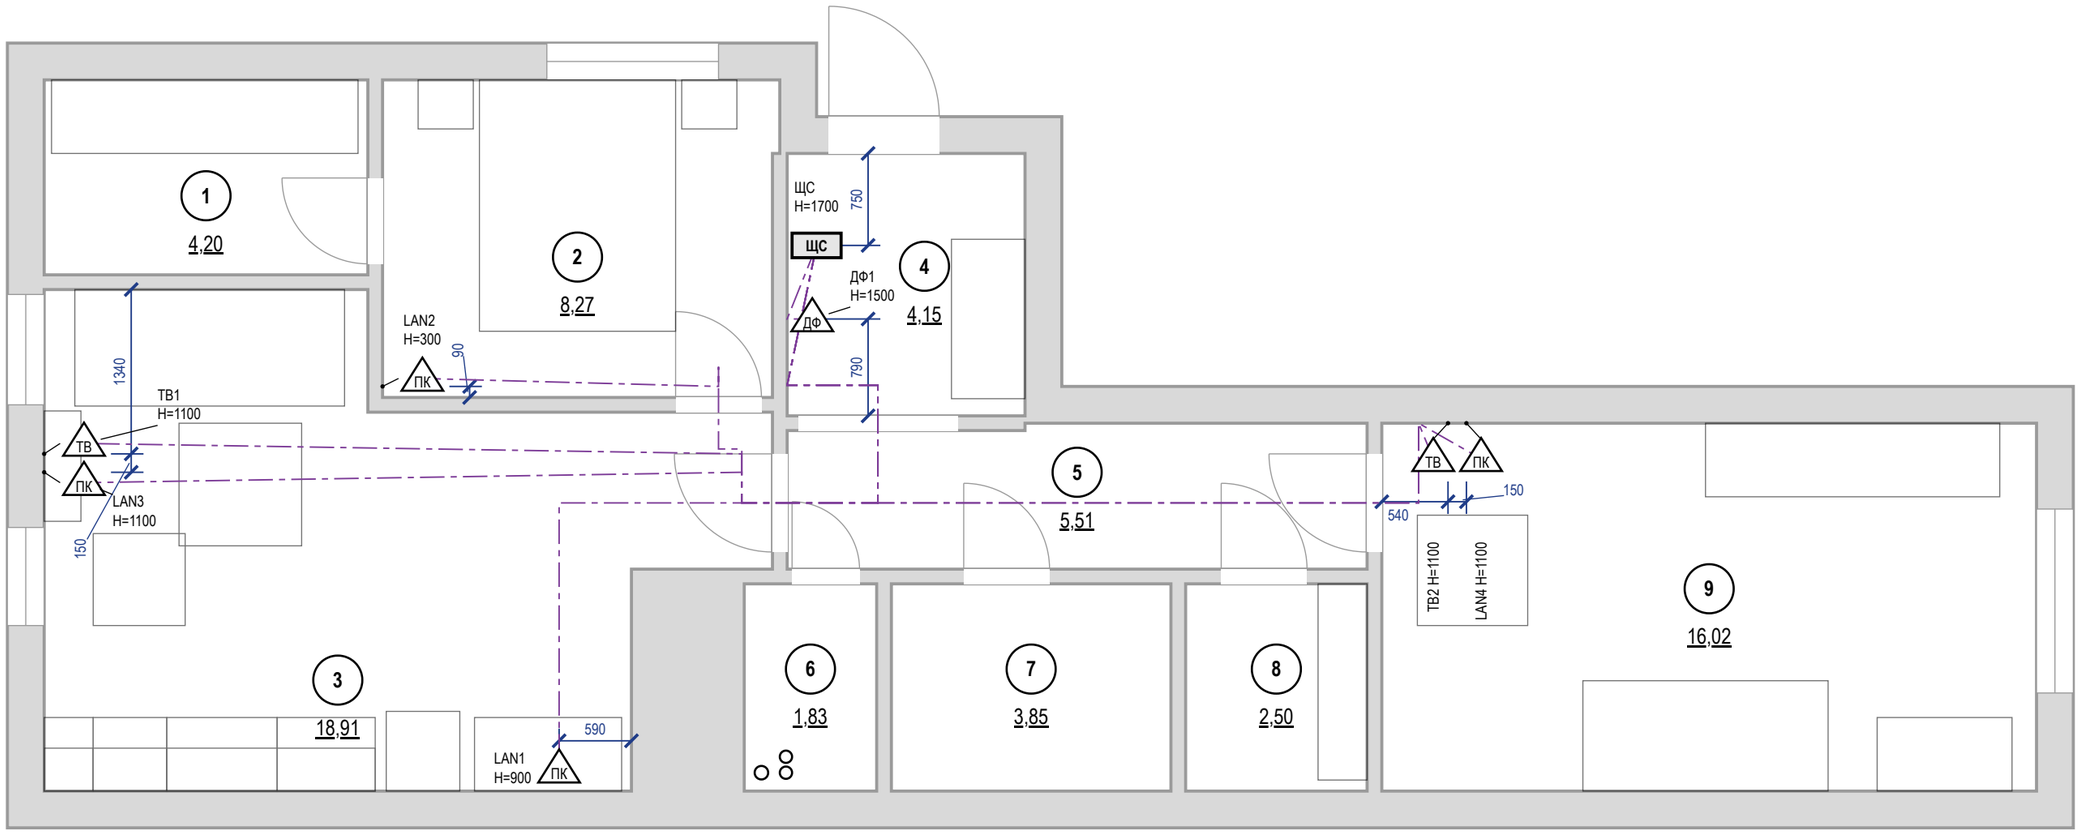

Примечания

1. За отметку 0,000 принят уровень чистого пола. Высоты Н — от чистого пола до оси изделия; привязки — от чистовой грани стены до оси механизма (у рамки на несколько постов — до оси рамки).
2. Высота установки, не указанная на плане: розетки LAN и ТВ — 300 мм от чистого пола.
3. Слаботочные кабели — отдельно от силовых: в своей трубе или лотке, при параллельной прокладке не ближе 100 мм к силовым, пересечения под прямым углом; каждую точку — отдельным кабелем от ЩС без скруток.
4. Трассы на листе — принципиальные; фактические зафиксировать исполнительной схемой до закрытия отделкой. Силовые линии, УЗО 30 мА, ДСУП, кабель нг(А)-LS — по листам розеток и щита.
5. Проект силовой части и расчёт токов КЗ — по проекту ЭОМ; слаботочная часть согласуется с провайдером и управляющей компанией (домофон, коллективное ТВ).

Условные обозначения

- ЩС — щит слаботочный: ввод провайдера, роутер, коммутатор
- ПК — розетка компьютерная RJ45
- ТВ — розетка телевизионная
- ДФ — трубка или монитор домофона
- кабель от ЩС до точки, отдельным лучом
- мебель и сантехприборы — подложка
- стояк: К1 — канализация, В1 — ХВС, Т3 — ГВС
- 1 — номер помещения, площадь м²


	Лист	№ док.	Подпись	Дата
Дизайнер	Кырлан А.С.			14.11.26
Проверил				
Н. контр.				
Утв.				

Проект: Квартира 65 м² — М 1:50

План слаботочных сетей

Стадия	Лист	Листов
П	47	105

План освещения (М 1:50)

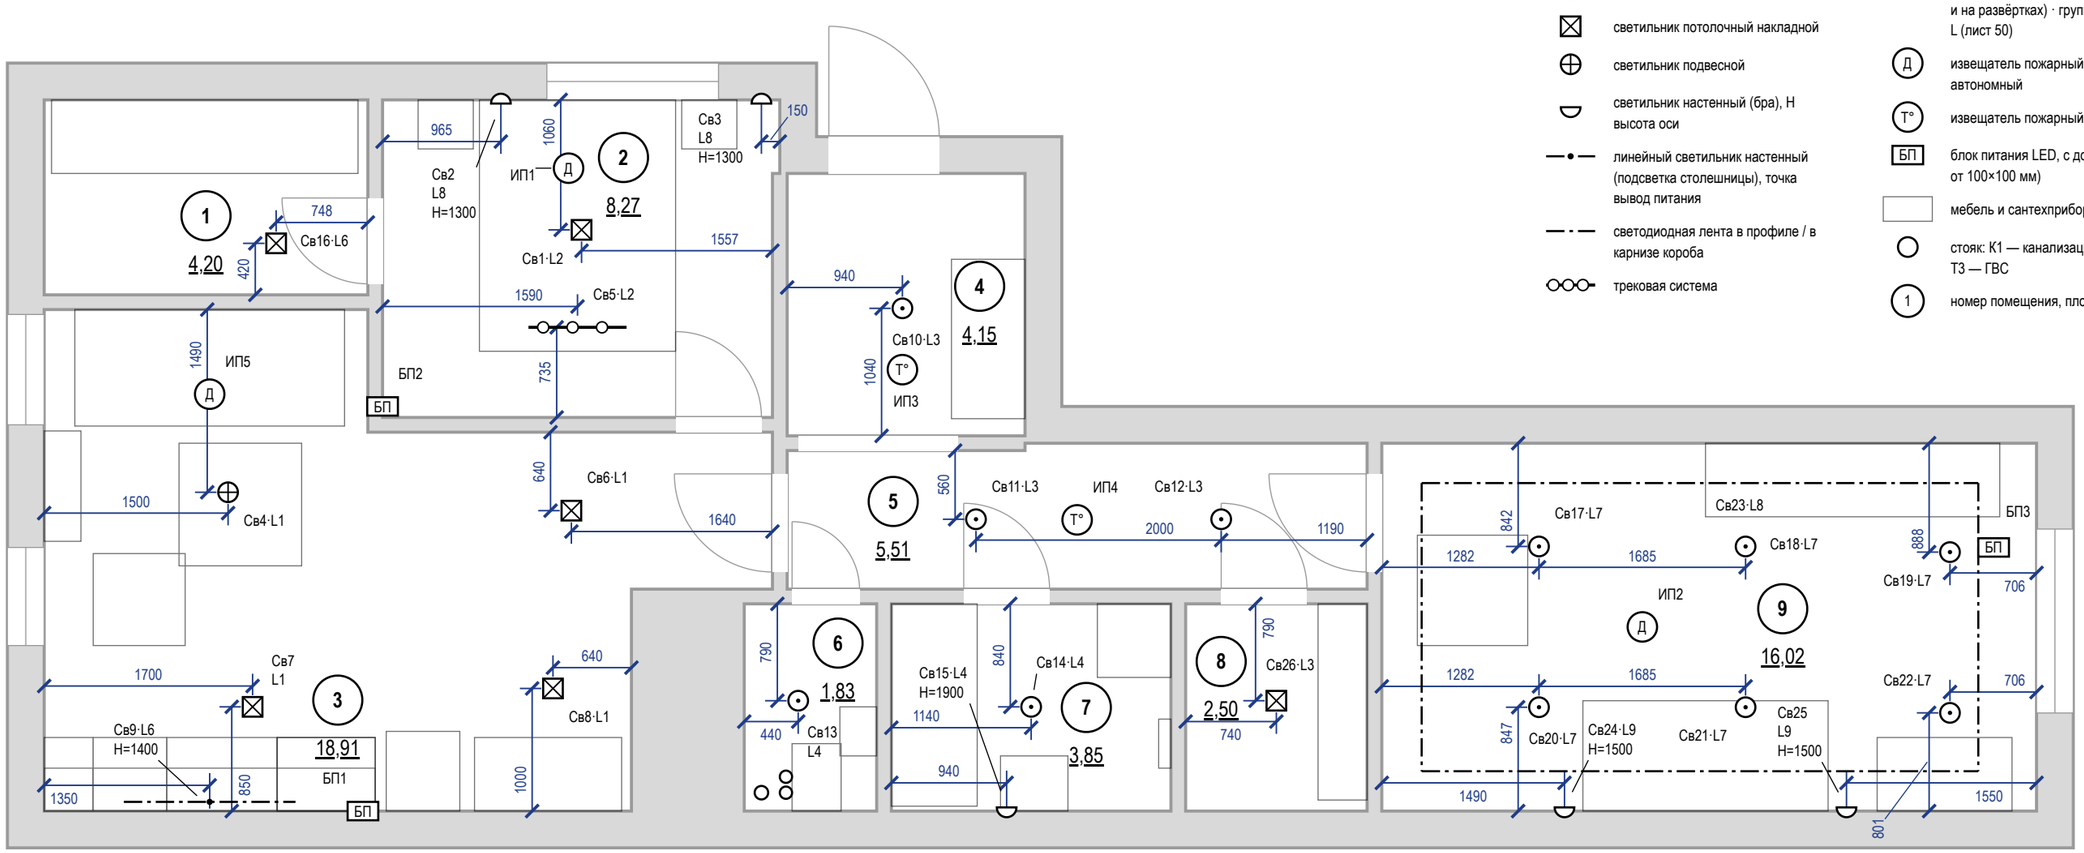

Условные обозначения

- светильник встраиваемый точечный
- светильник потолочный накладной
- светильник подвесной
- светильник настенный (бра), H высота оси
- линейный светильник настенный (подсветка столешницы), точка вывод питания
- светодиодная лента в профиле / в карнизе короба
- трековая система
- Св1·L1 — марка светильника (как в ведомости и на развёртках) · группа включения L (лист 50)
- Д — извещатель пожарный дымовой автономный
- Т° — извещатель пожарный тепловой
- БП — блок питания LED, с доступом (люк от 100×100 мм)
- мебель и сантехприборы — подложка
- стояк: К1 — канализация, В1 — ХВС, Т3 — ГВС
- 1 — номер помещения, площадь м²

Примечания

1. За отметку 0,000 принят уровень чистого пола. Высоты H — от чистого пола до оси изделия; привязки — от чистовой грани стены до оси механизма (у рамки на несколько постов — до оси рамки).
2. Высота установки, не указанная на плане: светильники — на потолке; настенные — по отметке H у знака. Привязки — до оси светильника от чистовой грани стены, по рядам.
3. Во влажных помещениях — светильники не ниже IP44; в зонах 0–2 ванной — по ГОСТ Р 50571.7.701-2024 (зона 1 — IPX5).
4. LED-лента в карнизе подсветки короба — по линии карниза с плана потолков; блок питания — в люке короба (БП на плане), питание ленты длиннее 5 м — с двух концов.
5. Розеточные и мокрые линии — через УЗО или дифавтомат с током утечки не более 30 мА (ПУЭ 7.1.79); в санузле выполнить ДСУП (ПУЭ 7.1.87–7.1.88).
6. Кабель — медный, исполнение нг(A)-LS (ГОСТ 31565-2012); скрытая прокладка только горизонтально и вертикально, фактические трассы зафиксировать исполнительной схемой до закрытия отделкой.
7. Расчёт нагрузок, токов КЗ, селективности и сечений — по проекту ЭОМ организации с допуском СРО; лист задаёт состав, расположение и группы.
8. Ведомость светильников (тип, количество, мощность, поток, Tц, Ra) — лист 49.

	Лист	№ док.	Подпись	Дата	Проект: Квартира 65 м²	М 1:50
Дизайнер	Кырлан А.С.			14.11.26		
Проверил					План освещения	Стадия: П · Лист: 48 · Листов: 105
Н. контр.						
Утв.						

Параметры светильников для подбора

Поз.	Марки	Наименование	Установка	Кол.	P, Вт	Σ P, Вт	Ф, лм	Тц, К	Ra	Угол, °	IP	Дим.	Слой	Группа	Пом.
1	Св16	Потолочный накладной	на потолке, засветка стены	1	10	10	900	3000	90	—	20	—	общий	L6	1
2	Св1	Потолочный накладной	на потолке	1	36	36	3200	2700	90	—	20	—	общий	L2	2
3	Св5	Трековая система	на потолке	2	12	24	900	2700	90	—	20	—	общий	L2	2
4	Св2, Св3	Настенный (бра)	на стене, H=1300	2	4	8	250	2700	90	—	20	—	рабочий	L8	2
5	Св4	Подвесной	подвес	1	24	24	2400	3000	90	—	20	—	общий	L1	3
6	Св6	Потолочный накладной	на потолке	1	18	18	1800	3000	90	—	20	—	общий	L1	3
7	Св7	Потолочный накладной	на потолке	1	12	12	1100	3000	90	—	20	—	общий	L1	3
8	Св8	Потолочный накладной	на потолке	1	12	12	1000	4000	90	—	20	—	общий	L1	3
9	Св9	Линейный настенный	под верхними шкафами, H=1400	1	18	18	1300	3000	90	—	20	—	рабочий	L6	3
10	Св10–Св12	Встраиваемый точечный	в ГКЛ, корпус ≤ 70 мм	3	9	27	800	3000	90	—	20	—	общий	L3	4, 5
11	Св13	Встраиваемый точечный	в ГКЛ, корпус ≤ 70 мм	1	6	6	500	3000	90	—	20	—	общий	L4	6
12	Св14	Встраиваемый точечный	в ГКЛ, корпус ≤ 70 мм	1	9	9	700	3000	90	—	44	—	общий	L4	7
13	Св15	Настенный (бра)	над зеркалом, H=1900	1	6	6	400	3000	90	—	44	—	рабочий	L4	7
14	Св26	Потолочный накладной	на потолке	1	9	9	600	3000	90	—	20	—	общий	L3	8
15	Св17–Св22	Встраиваемый точечный	в ГКЛ, корпус ≤ 70 мм	6	12	72	1050	2700	90	—	20	—	общий	L7	9
16	Св23	Лента светодиодная 24 В	в карнизе короба, профиль с рассеивателем	13,8 м	9,6/м	132,3	900/м	2700	90	—	20	да	акцентный	L8	9
17	Св24, Св25	Настенный (бра)	на стене, H=1500	2	6	12	400	2700	90	60	20	—	рабочий	L9	9
		Итого		**26 шт + 13,8 м**		**435,3**									

LED-ленты, линейные светильники и блоки питания


Марка	Пом.	L, м	U, В	Вт/м	Σ P, Вт	БП	P БП, Вт	Загр., %	Питание	Доступ к БП
Св5	2	0,8	24	—	24	БП2	60	40	встроенный ввод	H=2300
—	3	2,5	24	—	18	БП1	60	30	встроенный ввод	H=2300
Св23	9	13,8	24	9,6	132,3	БП3	200	66	с двух концов	люк 300×300 в коробе потолка ПТ3

Примечания

1. Позиции и марки Св — те же, что на плане освещения (лист 48); группы L — по плану выключателей (лист 50).
2. Модели светильников не выбраны: лист — техническое задание на подбор. Модель по строке таблицы: поток, Тц, Ra, угол, IP и регулировка яркости не хуже указанных, мощность не больше; встраиваемые — под глубину короба (графа «Установка»). IP 20 — сухие помещения. После выбора моделей (артикул, производитель) лист выпускается как «Спецификация светильников».
3. Длина LED-ленты в карнизе — по линии карниза плана потолков (лист 40); Σ P = Вт/м × длина. Блок питания загружен не больше чем на 80 %; лента 24 В длиннее 10 м питается с двух концов; доступ к блоку питания — люк ревизии 300×300 мм или место, указанное в таблице.
4. В пом. 9 свет включается клавишами групп — лист 50.
5. Мощность и поток в таблице — требования к подбору (поток не меньше, мощность не больше указанных); после выбора модели — по её паспорту, Σ P — установленная мощность освещения. Оценка освещённости — на плане освещения; это не светотехнический расчёт.

	Лист	№ док.	Подпись	Дата	Проект: Квартира 65 м²			
Дизайнер	Кырлан А.С.			14.11.26	Техническое задание на подбор светильников	Стадия	Лист	Листов
Проверил						П	49	105
Н. контр.								
Утв.								

План выключателей (М 1:50)

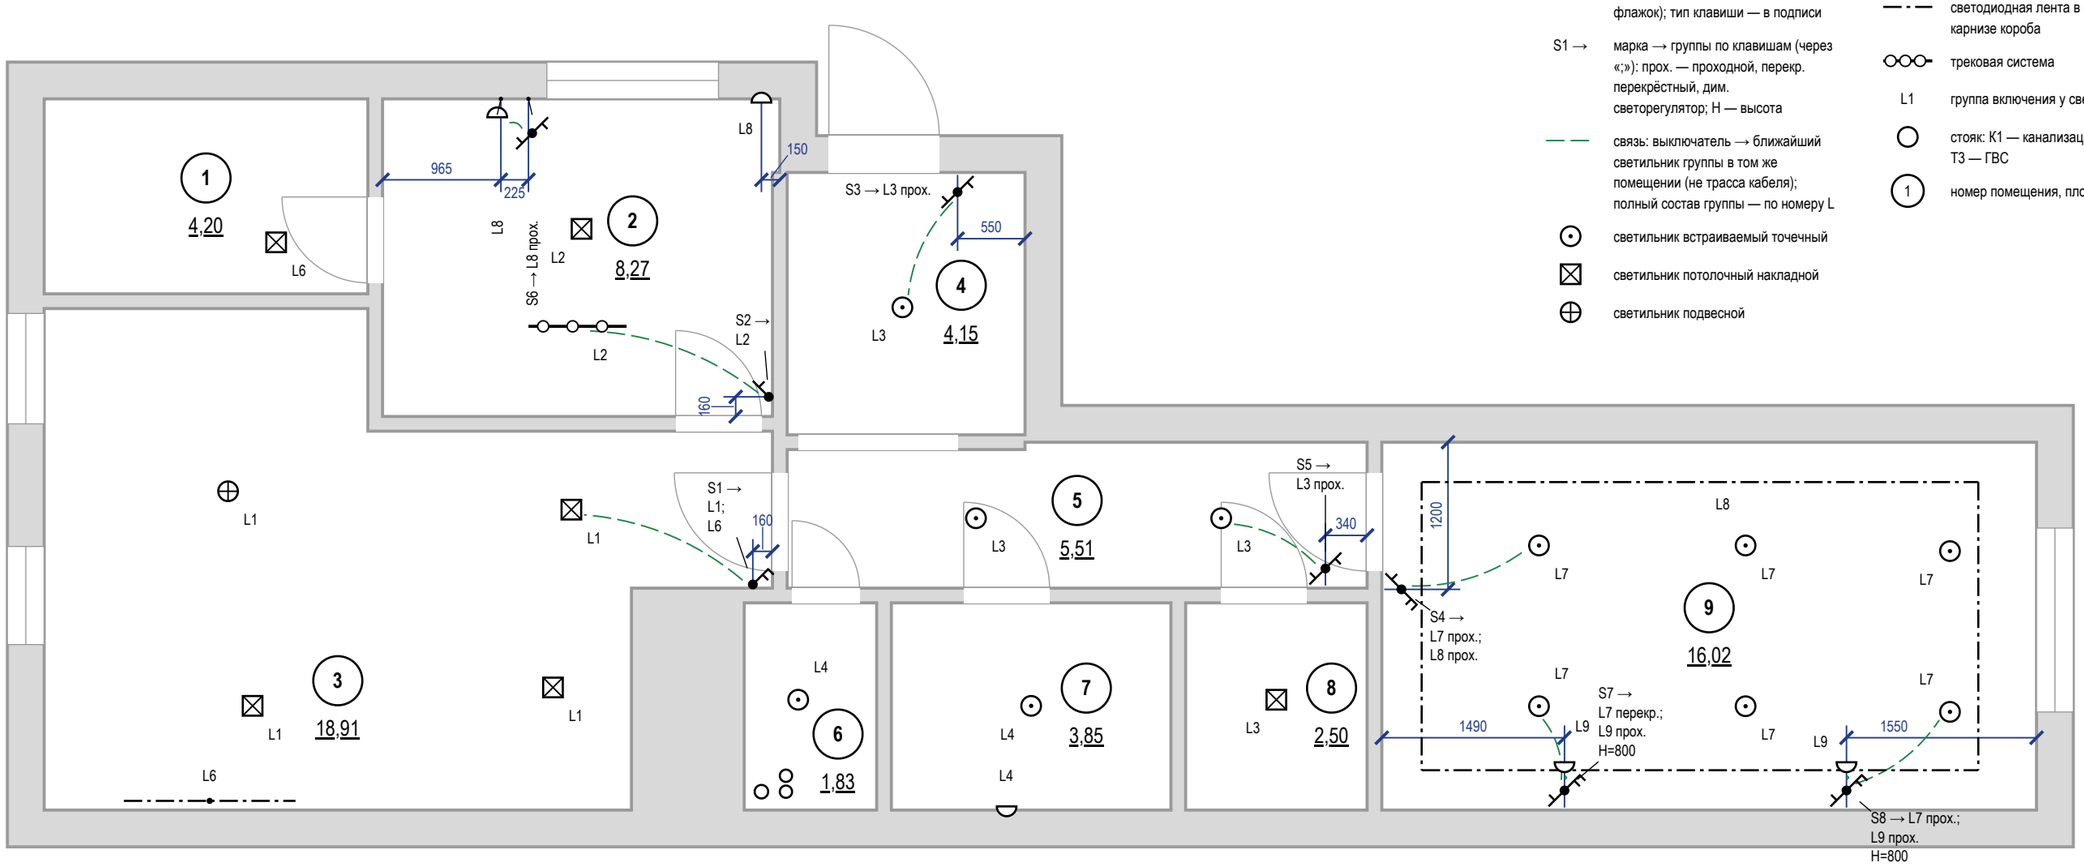

Условные обозначения


- выключатель одноклавишный
- выключатель двухклавишный (флажков — по числу клавиш)
- выключатель с проходной или перекрёстной клавишей (обратный флажок); тип клавиши — в подписи
- S1 → — марка → группы по клавишам (через «;»): прох. — проходной, перекр. перекрёстный, дим. светорегулятор; H — высота
- связь: выключатель → ближайший светильник группы в том же помещении (не трасса кабеля); полный состав группы — по номеру L
- светильник встраиваемый точечный
- светильник потолочный накладной
- светильник подвесной
- светильник настенный (бра), H высота оси
- линейный светильник настенный (подсветка столешницы), точка вывод питания
- светодиодная лента в профиле / в карнизе короба
- трековая система
- L1 — группа включения у светильника
- стояк: К1 — канализация, В1 — ХВС, Т3 — ГВС
- 1 — номер помещения, площадь м²

Примечания

1. За отметку 0,000 принят уровень чистого пола. Высоты H — от чистого пола до оси изделия; привязки — от чистовой грани стены до оси механизма (у рамки на несколько постов — до оси рамки).
2. Высота установки, не указанная на плане: выключатели — 900 мм от чистого пола (у кровати и другие — H у марки), со стороны дверной ручки (ПУЭ 7.1.51).
3. Какой выключатель какие светильники включает — по номеру группы L: у выключателя (S1 → L1; L2 — клавиши по порядку) и у каждого светильника. Пунктир подсказка к ближайшему светильнику группы в том же помещении (не дальше 3 м), это не трасса кабеля; выключатель за стеной (у двери санузла) и далёкая группа — только номер группы.
4. Группы из нескольких мест (L8 — S4, S6; L3 — S3, S5; L7 — S4, S7, S8; L9 — S7, S8): на крайних местах — проходные клавиши, на промежуточных — перекрёстные; механизмы — в ведомости изделий.
5. Вентиляторы санузлов (выводы ЭВ на плане розеток) включаются вместе с основным светом помещения, отключаются с задержкой — таймер выбега в вентиляторе.
6. Розеточные и мокрые линии — через УЗО или дифавтомат с током утечки не более 30 мА (ПУЭ 7.1.79); в санузле выполнить ДСУП (ПУЭ 7.1.87–7.1.88).
7. Кабель — медный, исполнение нг(A)-LS (ГОСТ 31565-2012); скрытая прокладка только горизонтально и вертикально, фактические трассы зафиксировать исполнительной схемой до закрытия отделкой.
8. Расчёт нагрузок, токов КЗ, селективности и сечений — по проекту ЭОМ организации с допуском СРО; лист задаёт состав, расположение и группы.
9. Группы без выключателя: L4 — выключатель в исходных данных не задан; управление группой согласуется до монтажа.

	Лист	№ док.	Подпись	Дата	Проект: Квартира 65 м²			М 1:50
Дизайнер	Кырлан А.С.			14.11.26	Управление светильниками	Стадия	Лист	Листов
Проверил						П	50	105
Н. контр.								
Утв.								

План вентиляции (М 1:50)

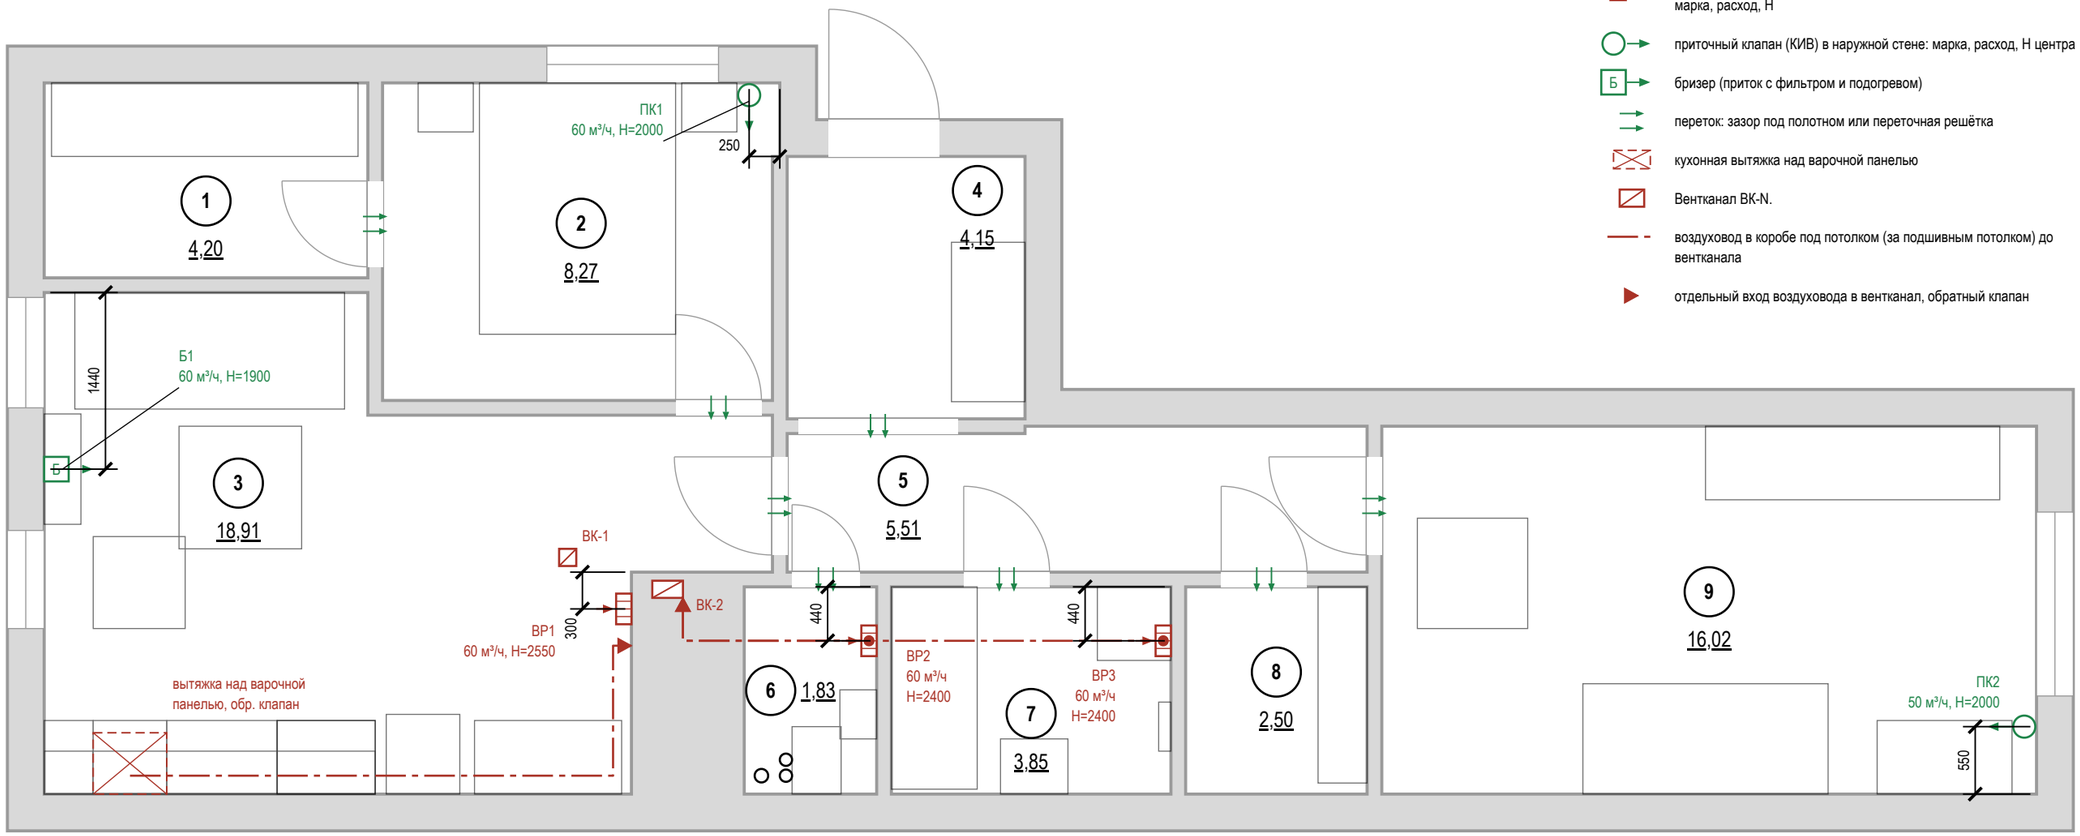

Условные обозначения

- стояк: К1 — канализация, В1 — ХВС, Т3 — ГВС
- 1 — номер помещения, площадь м²
- вытяжная решётка в вентканал: марка, расход м³/ч, H центра от чистого пола
- вытяжная решётка с бытовым вентилятором и обратным клапаном: марка, расход, H
- приточный клапан (КИВ) в наружной стене: марка, расход, H центра
- Б — бризер (приток с фильтром и подогревом)
- переток: зазор под полотном или переточная решётка
- кухонная вытяжка над варочной панелью
- Вентканал ВК-N.
- воздуховод в коробе под потолком (за подшивным потолком) до вентканала
- отдельный вход воздуховода в вентканал, обратный клапан


Примечания

1. Расчёт систем ОВ и подбор оборудования — проектная организация с допуском СРО; лист даёт места, трассы и привязки.
2. Нормы вытяжки — СП 54.13330.2022 (Изм. 1, 2), табл. 7.1: кухня с электроплитой 60 м³/ч, с газовой 100; ванная и совмещённый санузел 50; уборная 25; гардеробная 0,2 ч⁻¹. Приток в жилые — 3 м³/ч на 1 м² (менее 20 м² общей площади на человека), иначе 30 м³/ч на человека.
3. Вентканалы и шахты не сужать, не переносить и не закрывать; вентилятор и кухонная вытяжка — через обратный клапан, без перекрытия естественной тяги; ВР2 — воздуховодом до ВК-2 ≈ 1,9 м, ВР3 — воздуховодом до ВК-2 ≈ 4,3 м в коробе под потолком.
4. Проектные расходы — не ниже нормы, вытяжка сведена с притоком вентиляторами мокрых помещений. Клапаны — в простенке у окна, центр 2000 мм, не над кроватью, не ближе 300 мм к стоякам отопления; типоразмер — на расход.
5. Кухонная вытяжка в воздухообмен не включена: воздуховод не менее Ø125 в коробе, вход в канал отдельный.
6. Переток — зазор под полотнами межкомнатных дверей или переточная решётка.
7. Кондиционирование заданием не предусмотрено; при установке трассы фреона и дренажа (не менее 40 мм/м, в К1 через сифон) и питание заложить до черновых работ.
8. Привязки оборудования — по паспортам приобретённых моделей, до черновых работ.
9. Привязки — до обмера: вентканалы ВК-N приняты проектировщиком, решётки и воздуховоды — от них. До черновых работ — обмер каналов и тяги, лист перевыпустить по факту.

	Лист	№ док.	Подпись	Дата	Проект: Квартира 65 м²	М 1:50		
Дизайнер	Кырлан А.С.			14.11.26	План вентиляции	Стадия	Лист	Листов
Проверил						П	51	105
Н. контр.								
Утв.								

выпуск 14.11.2026 № 3aed0ef730 · стр. 51 из 105

План отопления (М 1:50)

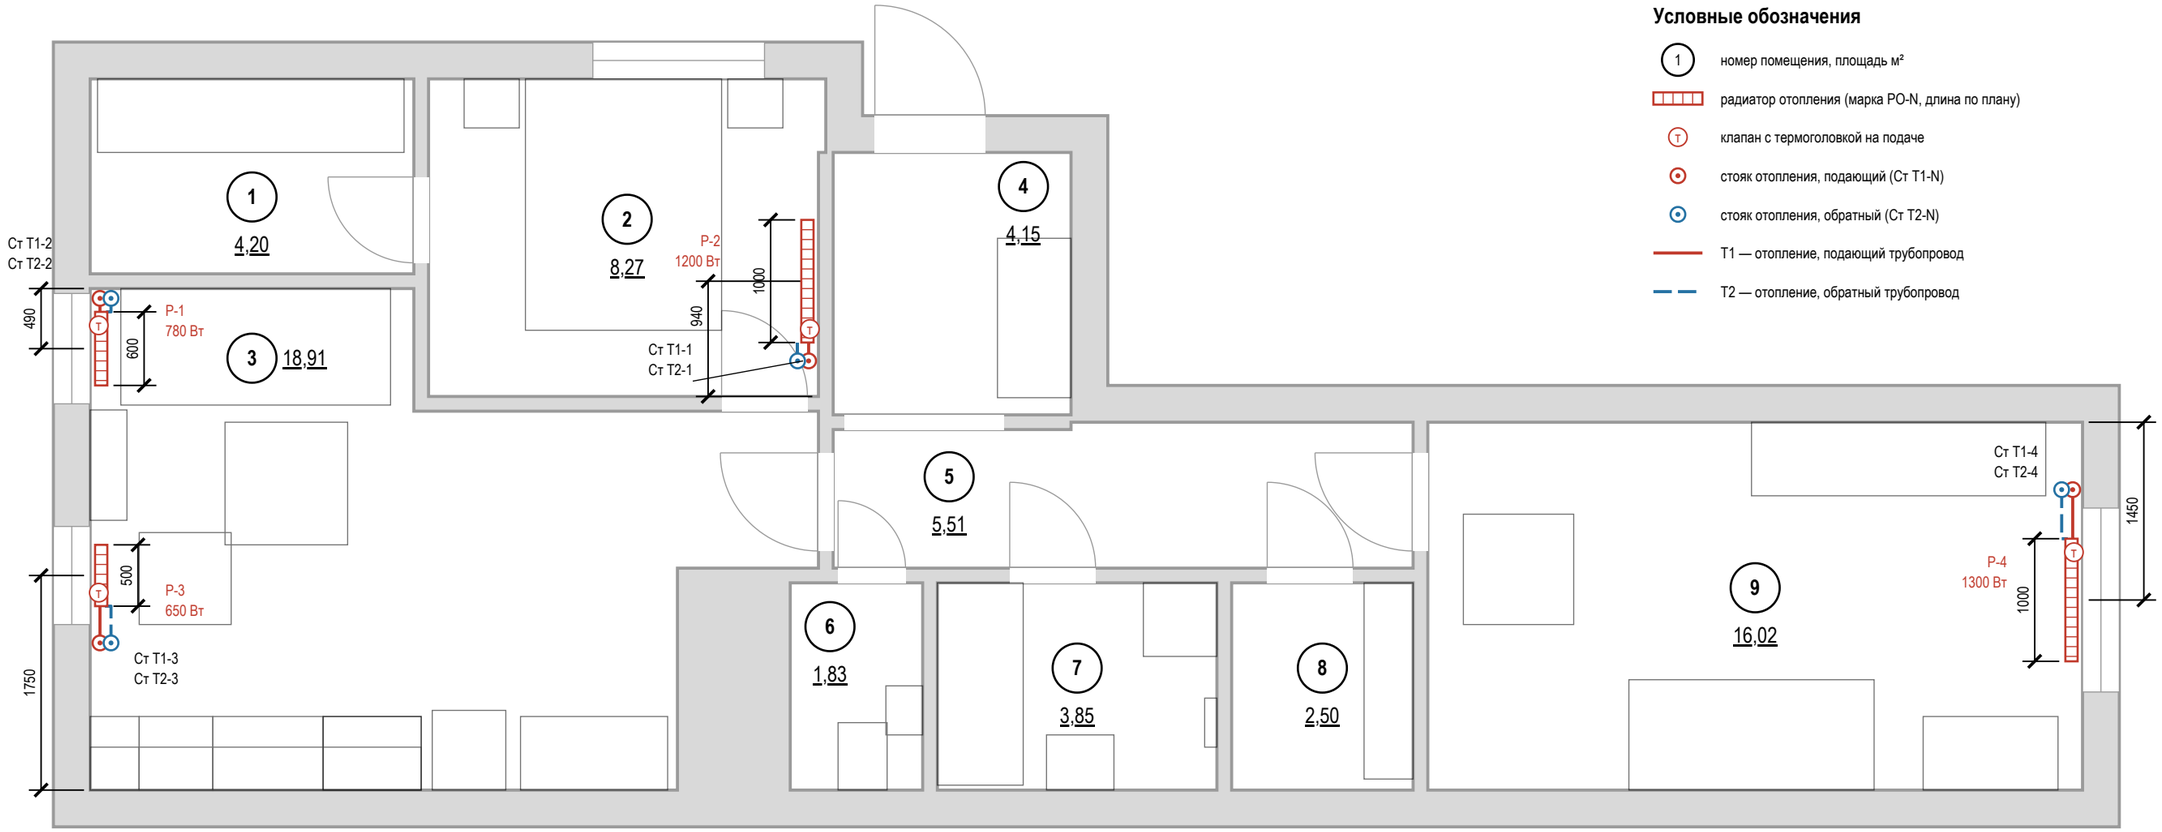

Условные обозначения

- 1 — номер помещения, площадь м²
- радиатор отопления (марка РО-N, длина по плану)
- клапан с термоголовкой на подаче
- стояк отопления, подающий (Ст Т1-N)
- стояк отопления, обратный (Ст Т2-N)
- Т1 — отопление, подающий трубопровод
- Т2 — отопление, обратный трубопровод

Примечания

1. Расчёт системы отопления, теплопотерь и подбор приборов — проектная организация с допуском СРО; лист даёт места и привязки.
2. Тип, длина и мощность радиаторов — по теплотехническому расчёту; лист задаёт места, зазоры и подключение.
3. Зазоры радиатора: низ не менее 100 мм от чистого пола, верх не менее 100 мм до подоконника, 30–50 мм от стены до задней панели; центр по оси окна с допуском ±20 мм. Верх до подоконника — 180 мм.
4. Радиаторы не закрывать глухими коробами и мебелью; перенос и замена приборов в многоквартирном доме — переустройство, согласование с управляющей организацией (ЖК РФ ст. 25–26); вынос на лоджию запрещён.
5. Трубы отопления через межквартирные стены не прокладывать (СП 51.13330.2011, п. 9.19); через перекрытия и перегородки — в гильзах.
6. Привязки приборов и подводок — по паспортам приобретённых радиаторов и клапанов, до черновых работ.
7. Привязки — до обмера: Стояки отопления в исходных данных не заданы: показаны у откосов окон и у торцов приборов, подводки — принципиально. До черновых работ — обмер стояков и паспорта приборов; лист перевыпустить по факту.
8. До закрытия отделкой трубопроводы отопления испытать гидростатическим давлением с оформлением акта (СП 73.13330.2016, 7.2–7.3).

	Лист	№ док.	Подпись	Дата
Дизайнер	Кырлан А.С.			14.11.26
Проверил				
Н. контр.				
Утв.				

Проект: Квартира 65 м² — **М 1:50**

План отопления



Стадия	Лист	Листов
П	52	105

выпуск 14.11.2026 № 3aed0ef730 · стр. 52 из 105

Спецификация плинтусов


Наименование	Помещения	Длина, м (с запасом)
SX165, h = 69 мм, крепление к стене, окраска в цвет Tikkurila V503	1	9
SX165, h = 69 мм, крепление к стене, окраска в цвет NCS S 0300-N	2, 3, 4, 5, 8	53
SX165, h = 69 мм, крепление к стене, окраска в цвет Farrow & Ball No. 241	9	18

Экспликация полов

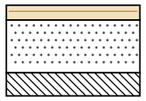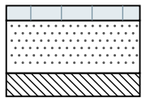Номер помещения	Тип пола	Схема пола	Данные элементов пола (наименование, толщина, основание), мм	Площадь, м²
1, 2, 3, 8, 9	1		Инженерная доска на клею — 14 Стяжка ЦПС М200 — 50 Плита перекрытия Всего 64 мм; ЧП ±0,000, верх плиты −0,064	49,90
4, 5	2		Керамогранит на клею С2 TE S1 — 14 Стяжка ЦПС М200 — 50 Плита перекрытия Всего 64 мм; ЧП ±0,000, верх плиты −0,064	9,66
6, 7	3		Керамогранит на клею С2 TE S1 — 14 Гидроизоляция обмазочная, 2 слоя, с заведением на стены 200 мм — 2 Стяжка ЦПС М200 — 33 Плита перекрытия Всего 49 мм; ЧП −0,015, верх плиты −0,064	5,68
			Итого	**65,24**

Отметки по высоте

±0,000 чистый пол пом. 1–5, 8, 9; отсчёт высот
−0,015 чистый пол пом. 6, 7, ниже на 15 мм
−0,064 верх плиты — расчёт, не замер (задание на обмер)
сущ. пол снимается до плиты; не замерен (задание на обмер)

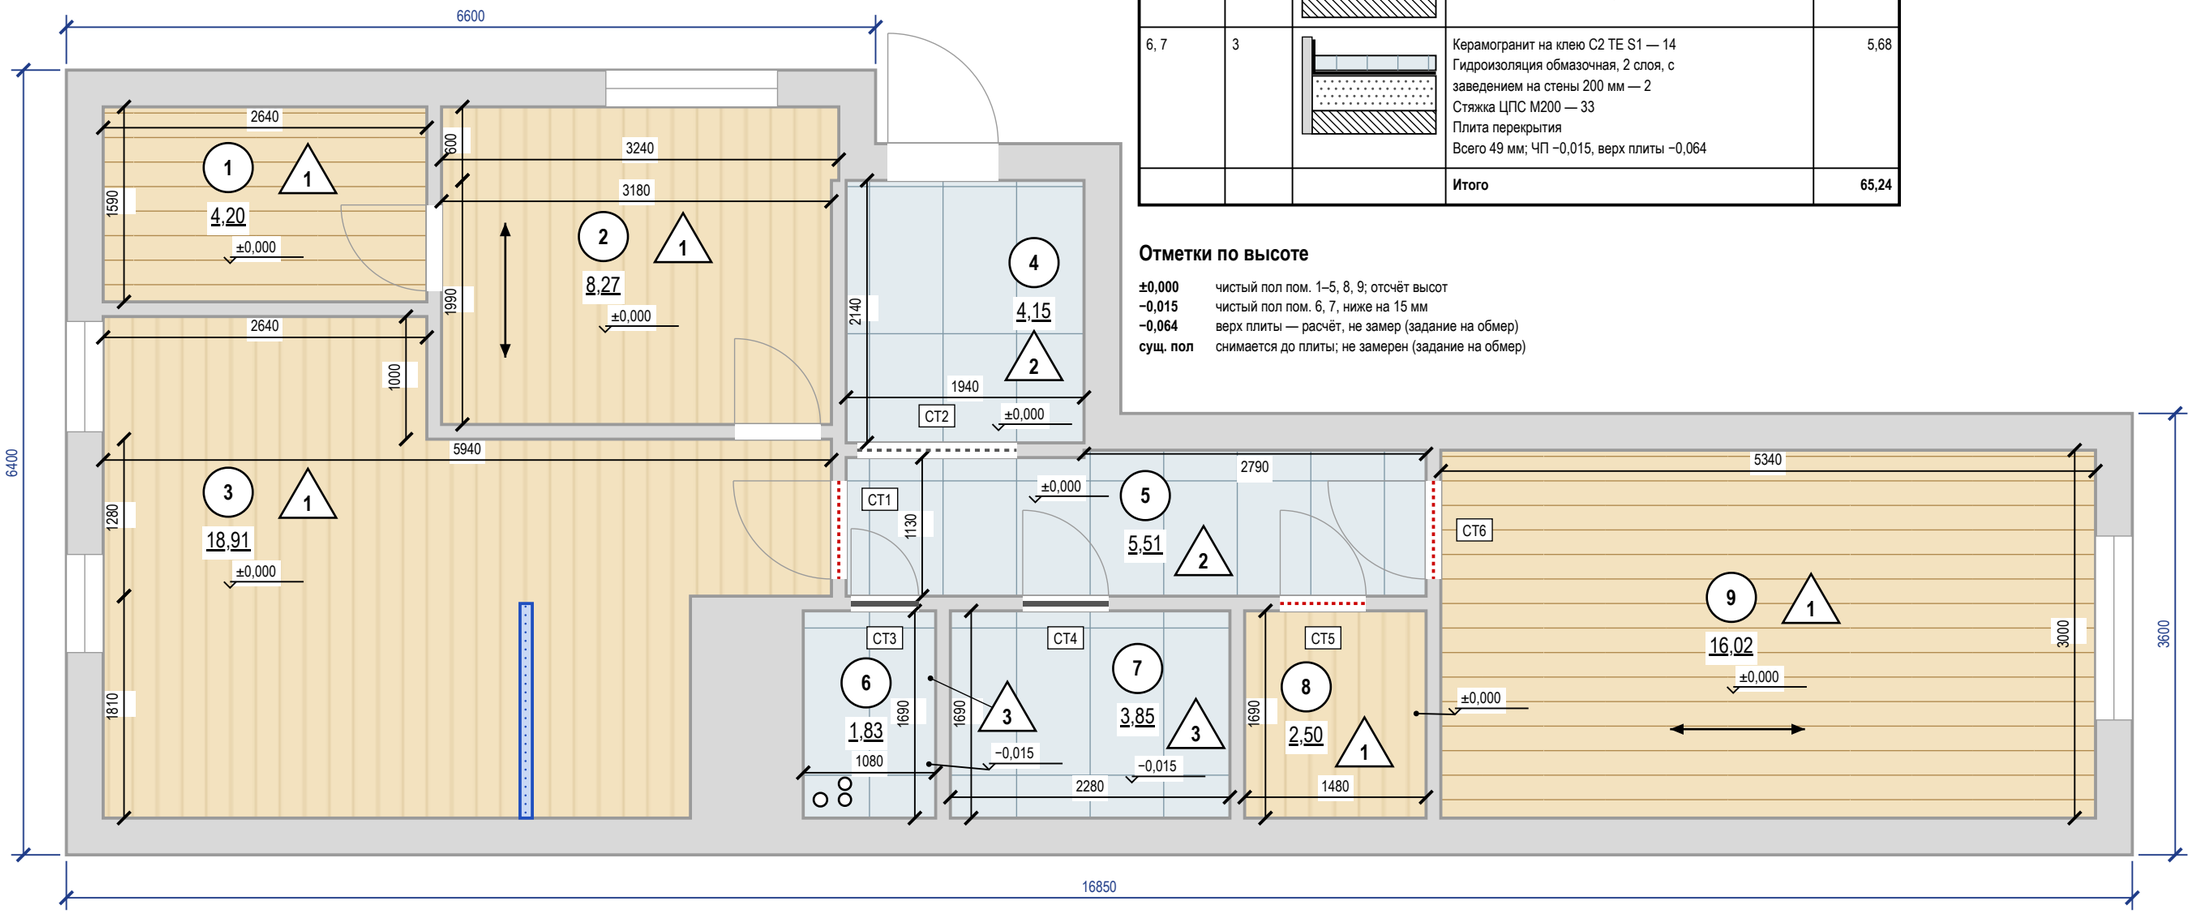


Примечания


1. За отметку ±0,000 принят чистый пол, не существующий (блок отметок). Площади — по чистым размерам помещений, м²; размеры — в мм.
2. Стык разнотипных покрытий — по оси дверного полотна (под полотном в закрытом положении); решение стыка — по ведомости стыков.
3. Размеры помещений в свету (ширина × длина, мм), не поместившиеся на плане: пом. 3 — 2640 × 1000, 5940 × 1280, 4790 × 1810; пом. 5 — 2790 × 60, 4730 × 1130.
4. Пол санузлов ниже смежных помещений на 15 мм за счёт меньшей толщины стяжки (верх плиты общий — по экспликации полов); гидроизоляция по стяжке с заведением на стены не менее 200 мм (СП 29.13330.2011, п. 7.2), до облицовки — тест проливом и акт скрытых работ.
5. Выпуски канализации с уклоном и трассы водоснабжения — в слое засыпки под стяжкой (по экспликации полов); отметки, уклоны и прочистки — по листу разводки ВК 28.
6. Звукоизоляционный слой под стяжкой проектом не предусмотрен (стяжка по плите): приведённый уровень ударного шума перекрытия с полом Lnw не более 60 дБ (СП 51.13330.2011, табл. 2) подтвердить по данным дома; при превышении — плавающая стяжка по звукоизоляции с демпферной лентой по контуру и у стояков, пирог пересчитать.
7. Штучные покрытия (инженерная доска): направление — по стрелке; влажность основания по СМ не более 2,0 % (по ТУ изготовителя).
8. Ровность основания — просвет под 2-метровой рейкой не более 2 мм: пом. 1, 2, 3, 8, 9 (инженерная доска), пом. 4, 5, 6, 7 (керамогранит); проверить до укладки покрытия (СП 71.13330.2017, табл. 8.5).
9. Сетка на плитке — условная, в размер формата; точка старта и раскладка — по листу раскладки плитки.
10. Узор покрытия (заливка-код типа пола) прерывается под надписями — площадями помещений и отметками чистого пола.
11. Пироги полов — по экспликации полов: слои сверху вниз, толщины в мм; гидроизоляция мокрых зон — в пироге и в ведомости отделки; схема пола — без масштаба.

	Лист	№ док.	Подпись	Дата	Проект: Квартира 65 м²			М 1:50
Дизайнер	Кырлан А.С.			14.11.26	План покрытий пола	Стадия	Лист	Листов
Проверил						П	53	105
Н. контр.								
Утв.								

Фрагмент 1. Санузел (пом. 6). Пол 600×1200, шов 2 мм (М 1:20)

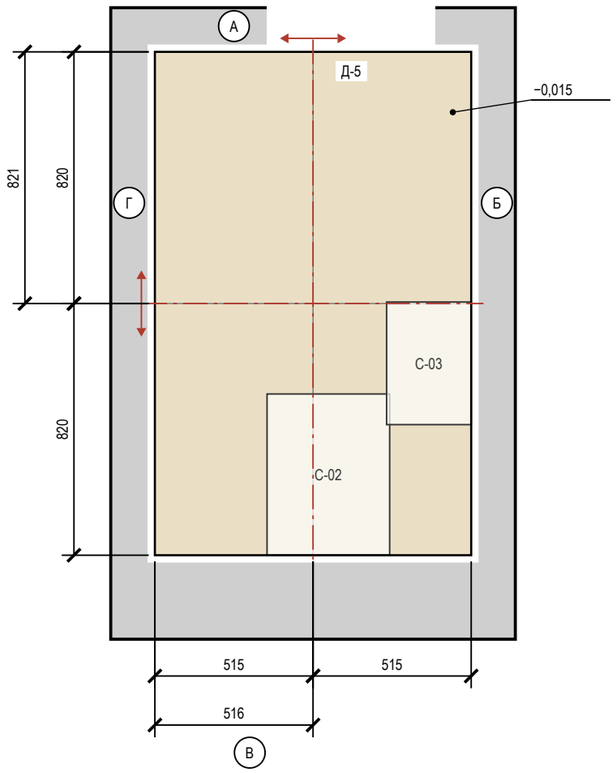

Фрагмент 2. Ванная (пом. 7). Пол 600×1200, шов 2 мм (М 1:20)

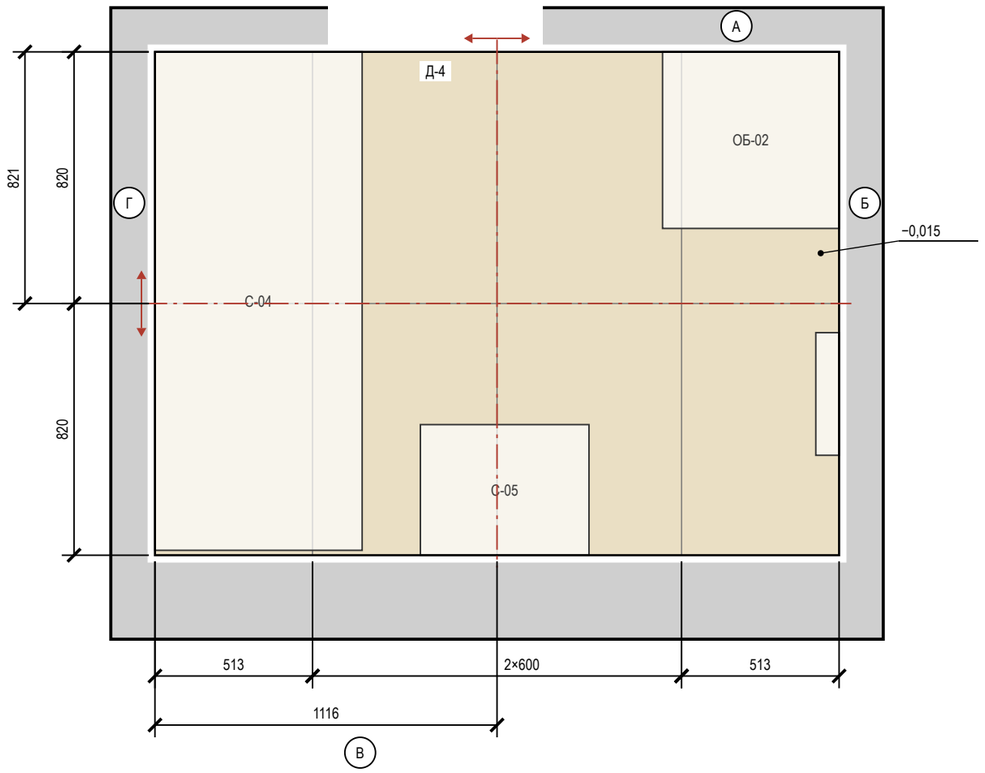

Условные обозначения

- плитка целая; тонкая линия — шов
- плитка с подрезкой (размер — на цепочке)
- ось старта; стрелки — направление укладки
- сантехприбор: габарит, высота по практике
- отметка чистого пола на полке выноски, м
- (А) обозначение стены А–Г (как на развёртках)

Ведомость плитки

Помещение, поверхность	Плитка, код	Формат	Шов	S, м²	Целых	Подр.	С запасом
Санузел, пол	SG501600R	600×1200	2	1,83	0	4	5
Санузел, стены А–Г	610010001195	1200×600	2	13,33	0	30	34
Ванная, пол	SG501600R	600×1200	2	3,85	0	8	9
Ванная, стены А–Г	610010001195	1200×600	2	19,29	0	40	44
Прихожая, пол	SG501600R	600×1200	2	4,15	0	8	9
Коридор, пол	SG501600R	600×1200	2	5,51	0	8	9
Итого 600×1200				**47,97**	**0**	**98**	**110**

Ведомость материалов

Материал	Класс, код	Норма расхода	Кол-во
Затирка	класс не задан	(a+b)/ab·шов·t·1,6	3,7 кг
Клей	С2 S1	1,2 кг/м²·мм, слой 5	36 кг (2 меш.)
Клей	С2	1,2 кг/м²·мм, слой 5	271 кг (11 меш.)
Гидроизоляция	обмазочная, 2 слоя: пол, стены по периметру и зоны замачивания	по ТУ	14,8 м²
Демпф. лента	по периметру пола из плитки		27,0 м


Примечания

1. Раскладка от чистовых размеров: стены санузлов теряют 10 + 5 + 9 = 24 мм на сторону (штукатурка, клей, плитка); подрезки — чистые, без шва.
2. Старт — от центра помещения (штрихпунктир, стрелки — направление укладки); размер старта — от чистовых стен Г и А.
3. Раскладка пола «Прихожая» и пола «Коридор» — на листе «Раскладка плитки. Прихожая. Коридор».
4. Калибр партии не задан — до укладки замерить (рабочий размер W, ГОСТ 13996-2019) и пересчитать подрезки.
5. Количество: целые по раскладке + по одной на подрезку, запас 10 %; один артикул — одна партия и тон. Исключены поддон, короб, проёмы и места за коробом; S — по чистым граням, как в ведомости отделки.
6. Клей С2 S1; С2 (ГОСТ Р 56387-2018), затирка класс не задан; расход — по ТУ выбранной марки.
7. Гидроизоляция: пол и стены 200 мм от ЧП; над ванной — до 2000 и 300 мм за борт (пом. 7) (см. развёртки); акт скрытых работ, пролив 24 ч.
8. Отметка чистого пола −0,015, порог 15 мм; стык с соседним покрытием — по оси полотна двери.


	Лист	№ док.	Подпись	Дата	Проект: Квартира 65 м²			М 1:20
Дизайнер	Кырлан А.С.			14.11.26				
Проверил					Раскладка плитки. Планы полов	Стадия	Лист	Листов
Н. контр.						П	54	105
Утв.								

выпуск 14.11.2026 № 3aed0ef730 · стр. 54 из 105

Фрагмент 1. Прихожая (пом. 4). Пол 600×1200, шов 2 мм (М 1:25)

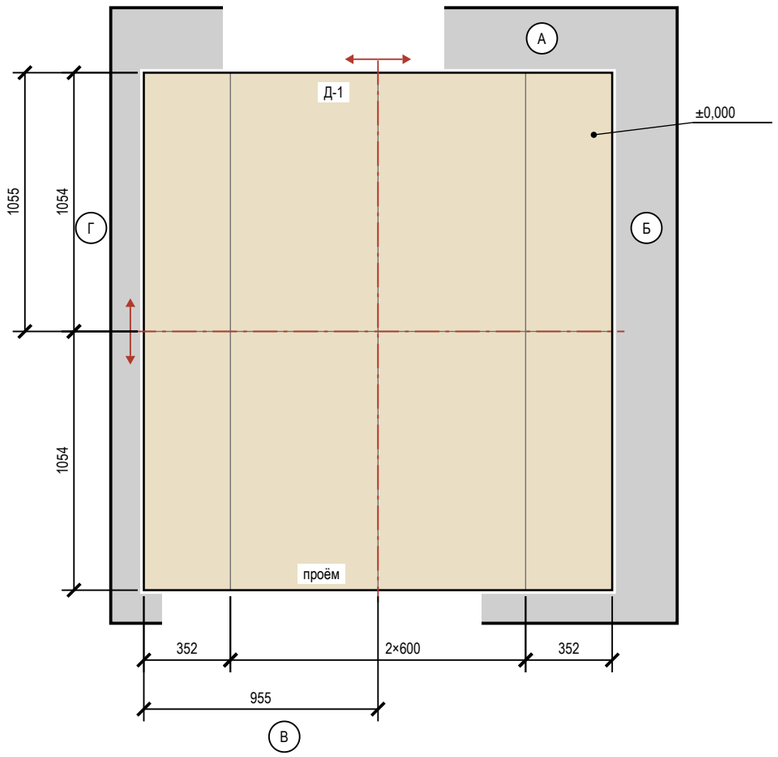

Фрагмент 2. Коридор (пом. 5). Пол 600×1200, шов 2 мм (М 1:25)

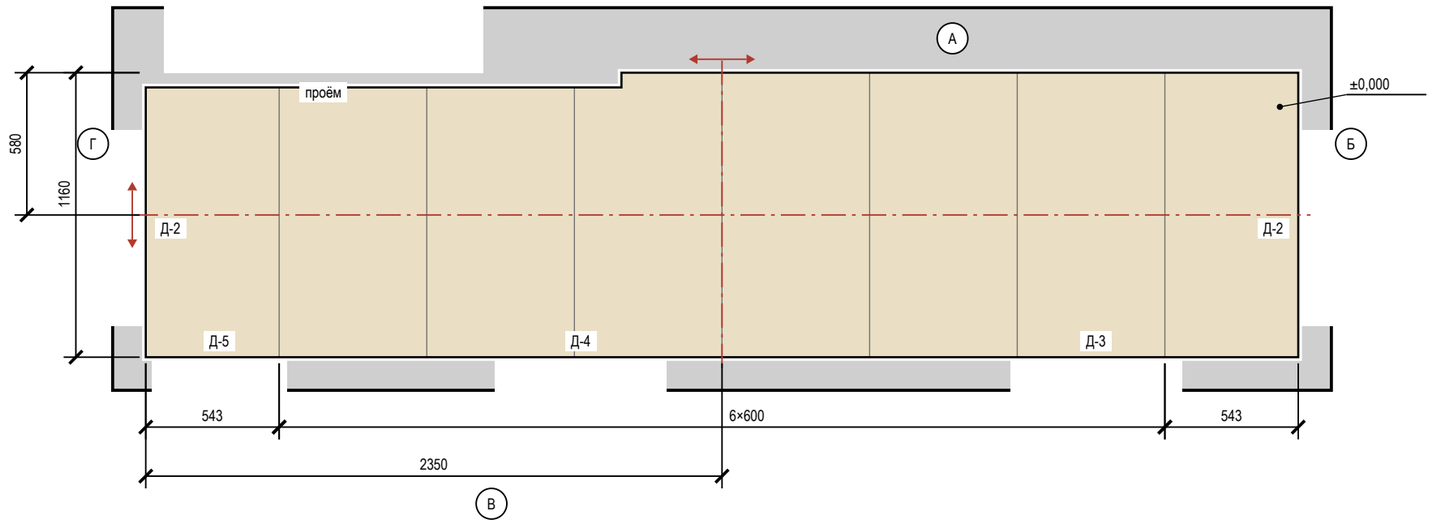

Условные обозначения

- плитка целая; тонкая линия — шов
- плитка с подрезкой (размер — на цепочке)
- ось старта; стрелки — направление укладки
- отметка чистого пола на полке выноски, м
- (А) обозначение стены А–Г (как на развёртках)

Подсчёт плитки


Поверхность	Формат	S, м²	Целых	Подр.	С запасом
Прихожая, пол	600×1200	4,15	0	8	9
Коридор, пол	600×1200	5,51	0	8	9

Примечания

1. Прихожая: керамогранит 600×1200, длинная сторона — вдоль стен Б и Г, шов 2 мм, прямая раскладка от центра. Стены окрашены: раскладка от чистового контура минус штукатурка и шпаклёвка 15 мм на сторону (принято); подрезки 352 / 1054 мм, срез — под плинтус.
2. Прихожая: деформационный зазор по периметру 8–10 мм под плинтусом; в проёмах — стык с соседним покрытием по оси полотна двери. Клей С2, затирка класс не задан.
3. Коридор: керамогранит 600×1200, длинная сторона — вдоль стен Б и Г, шов 2 мм, прямая раскладка от центра. Стены окрашены: раскладка от чистового контура минус штукатурка и шпаклёвка 15 мм на сторону (принято); подрезки 543 / 1160 мм, срез — под плинтус.
4. Коридор: деформационный зазор по периметру 8–10 мм под плинтусом; в проёмах — стык с соседним покрытием по оси полотна двери. Клей С2, затирка класс не задан.
5. Клей, затирка и итог по форматам — в ведомостях листа «Раскладка плитки. Планы полов».


	Лист	№ док.	Подпись	Дата	Проект: Квартира 65 м²			М 1:25
Дизайнер	Кырлан А.С.			14.11.26	Раскладка плитки. Прихожая. Коридор	Стадия	Лист	Листов
Проверил						П	55	105
Н. контр.								
Утв.								

Стена А (М 1:20)

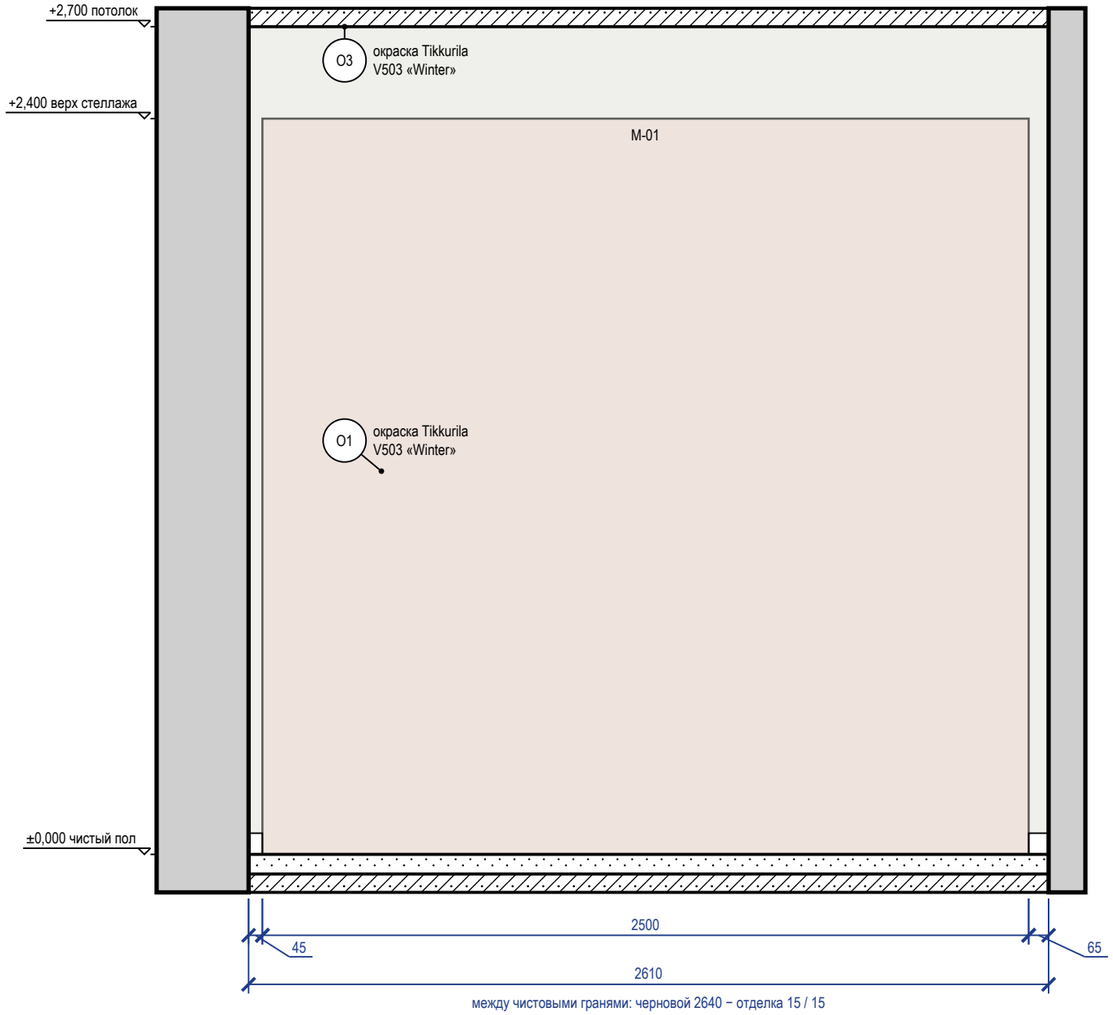

5 **Плинтус МДФ 69×16 мм у окрашенной стены по доске (ламинату) (М 1:5)**

Узел 5 — лист С13

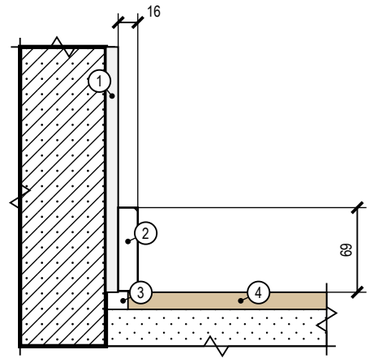


Поз.	Состав слоя, изделие
1	штукатурка, шпаклёвка Q3, окраска — по ведомости отделки
2	плинтус МДФ 69×16 под окраску в цвет стены; клей монтажный — к стене, не к полу
3	зазор покрытия у стены 8–10 мм закрывается плинтусом
4	инженерная доска на клею

Ведомость отделки (на листе)

Марка	Поверхность	Материал, изделие	Цвет, код	Кол.
О1	стены	окраска, Tikkurila Harmony, матовая, подготовка Q3	Tikkurila V503 «Winter»	7 м²
О2	плинтус	плинтус МДФ, Orac Decor Contour (Luxxus), h 69 мм, SX165	Tikkurila V503 «Winter»	0,1 м
О3	потолок	окраска, Tikkurila Anti-Reflex 2, глубокоматовая, подготовка Q3	Tikkurila V503 «Winter»	4,2 м²

Схема развёрток (М 1:50)

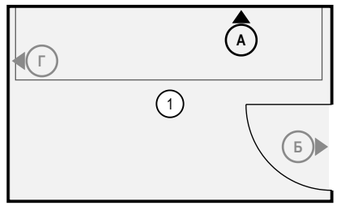

Ведомость изделий и проёмов (на листе)

Марка	Изделие, проём	На виде Ш×В, мм	Низ, мм
М-01	система хранения: штанги, полки, ящики	2500×2400	0


Примечания

1. Размеры — в мм от чистовых поверхностей стен; условные обозначения и общие указания — лист 14.


	Лист	№ док.	Подпись	Дата	Проект: Квартира 65 м²	М 1:20
Дизайнер	Кырлан А.С.			14.11.26	Развёртка стены А. Гардеробная (пом. 1)	Стадия: П; Лист: 56; Листов: 105
Проверил						
Н. контр.						
Утв.						

выпуск 14.11.2026 № 3aed0ef730 · стр. 56 из 105

Стена Б (М 1:20)

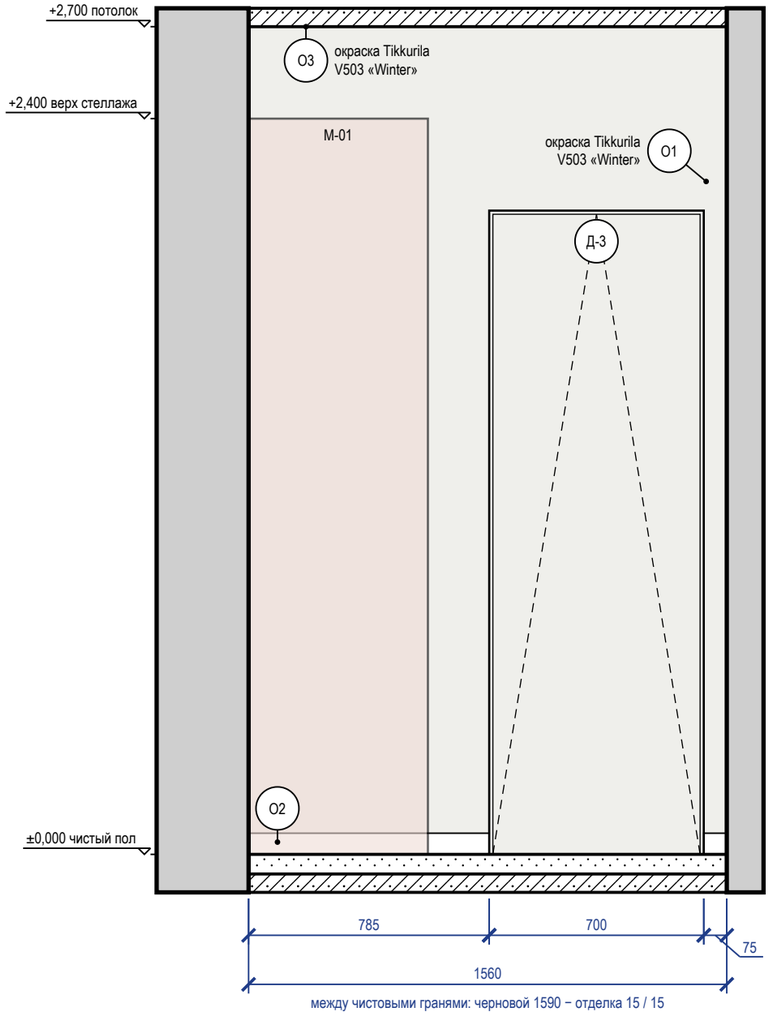

Стена Г (М 1:20)

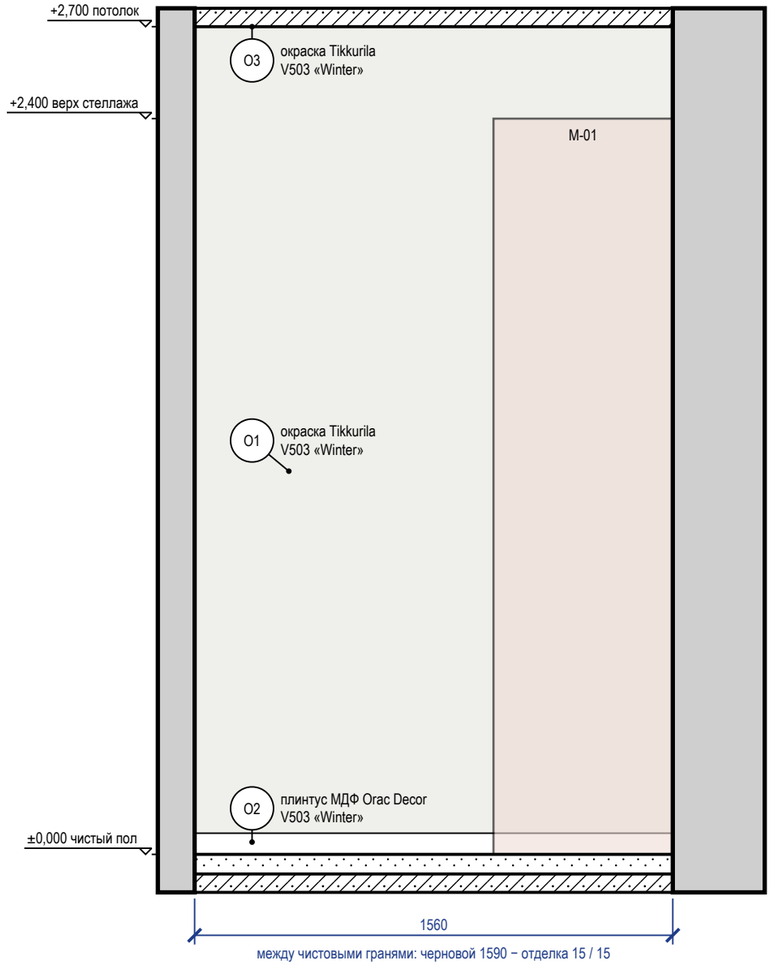


Ведомость отделки (на листе)

Марка	Поверхность	Материал, изделие	Цвет, код	Кол.
О1	стены	окраска, Tikkurila Harmony, матовая, подготовка Q3	Tikkurila V503 «Winter»	7 м²
О2	плинтус	плинтус МДФ, Orac Decor Contour (Luxxus), h 69 мм, SX165	Tikkurila V503 «Winter»	2,4 м
О3	потолок	окраска, Tikkurila Anti-Reflex 2, глубокоматовая, подготовка Q3	Tikkurila V503 «Winter»	4,2 м²

Стена Г — визуализация, лист 3



Схема развёрток (М 1:50)

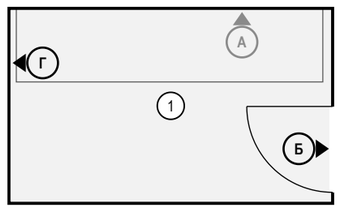

Ведомость изделий и проёмов (на листе)


Стена	Марка	Изделие, проём	На виде Ш×В, мм	Низ, мм
Б	М-01	система хранения: штанги, полки, ящики	585×2400	0
Б	Д-3	дверь скрытого монтажа	700×2100	0
Г	М-01	система хранения: штанги, полки, ящики	585×2400	0

Примечания

1. Размеры — в мм от чистовых поверхностей стен; условные обозначения и общие указания — лист 14.
2. Двери скрытого монтажа — полотно в плоскости стены, отделка стены по полотну, плинтус прерывается у короба (узел — на листе узлов).

	Лист	№ док.	Подпись	Дата	Проект: Квартира 65 м²			М 1:20
Дизайнер	Кырлан А.С.			14.11.26	Развёртки стен Б, Г. Гардеробная (пом. 1)	Стадия	Лист	Листов
Проверил						П	57	105
Н. контр.								
Утв.								

Стена А (М 1:20)

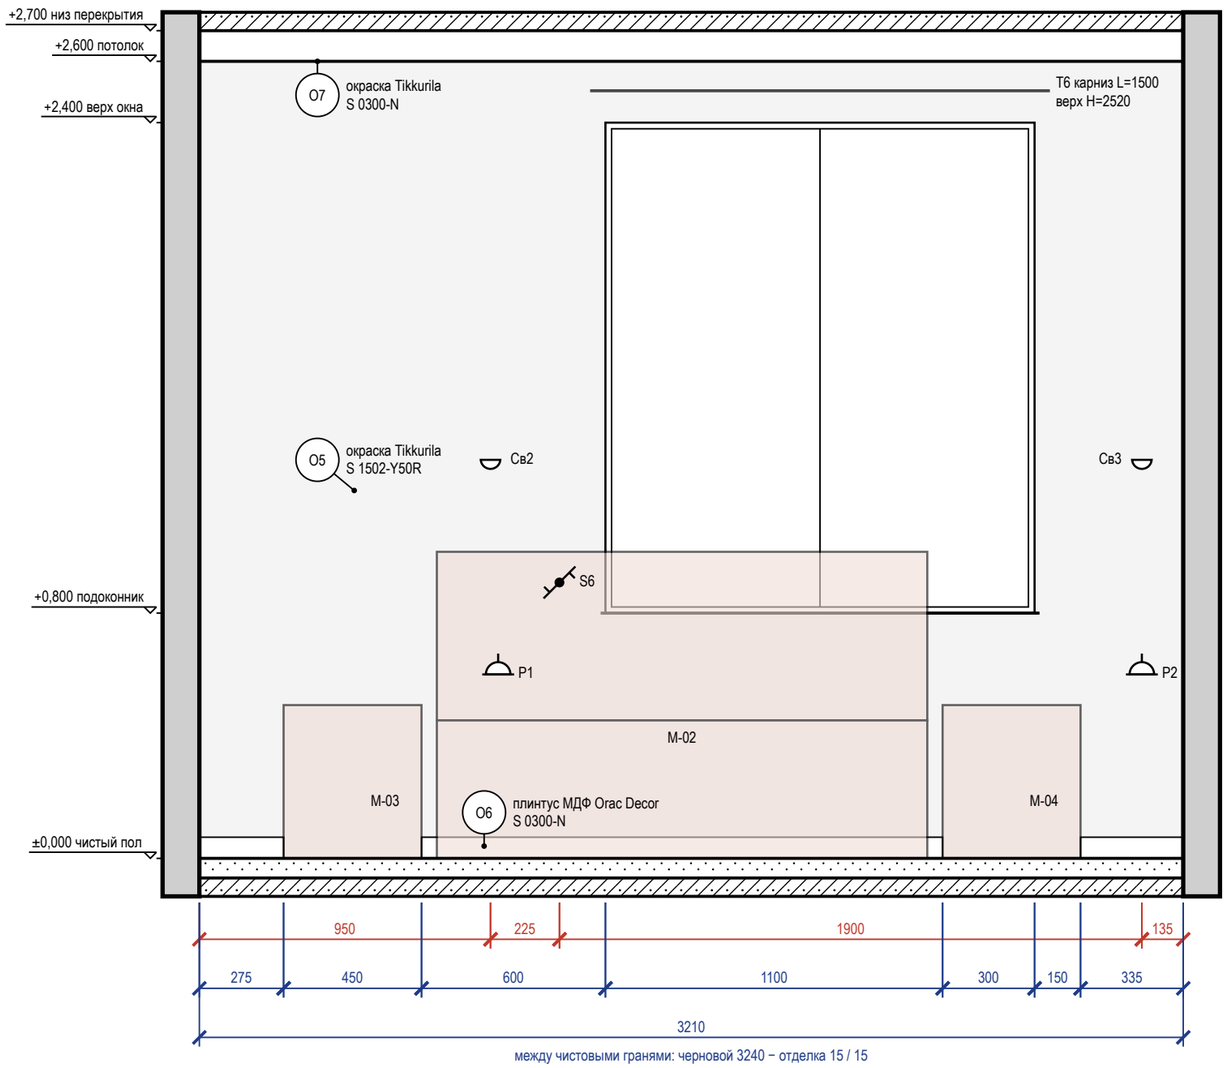


между чистовыми гранями: черновой 3240 − отделка 15 / 15

Стена А — визуализация, лист 4



Схема развёрток (М 1:50)

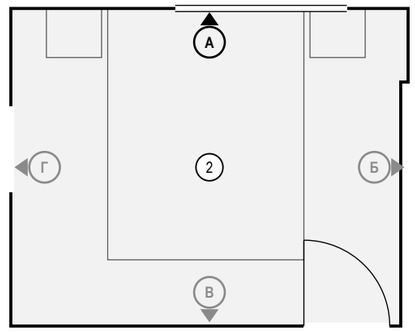

Ведомость точек и выводов

Марка	Что это	Гр.	H, мм	От угла, мм	Примечание
Св2	светильник настенный	1	1300	950	
P1	розетка	4	600	975	
S6	выключатель	1	900	1175	
P2	розетка	4	600	3075	
Св3	светильник настенный	1	1300	3075	

Ведомость отделки (на листе)

Марка	Поверхность	Материал, изделие	Цвет, код	Кол.
О5	стены	окраска, Tikkurila, глубокоматовая, подготовка Q3	NCS S 1502-Y50R	6,1 м²
О6	плинтус	плинтус МДФ, Orac Decor Contour (Luxxus), h 69 мм, SX165, шелковисто-матовая	NCS S 0300-N	2,3 м
О7	потолок	окраска, Tikkurila, глубокоматовая	NCS S 0300-N	8,3 м²

Ведомость изделий и проёмов (на листе)

Марка	Изделие, проём	На виде Ш×В, мм	Низ, мм
М-03	тумба прикроватная	450×500	0
М-02	кровать	1600×450	0
М-04	тумба прикроватная	450×500	0

Примечания

1. Размеры — в мм от чистовых поверхностей стен; условные обозначения и общие указания — лист 14.
2. Карнизы (шины) — по ведомости текстиля декоратора: длина L и верх H на развёртке — те же числа, что в ведомости; крепление — до окраски потолка.

	Лист	№ док.	Подпись	Дата
Дизайнер	Кырлан А.С.			14.11.26
Проверил				
Н. контр.				
Утв.				


Проект: Квартира 65 м² — М 1:20

Развёртка стены А. Спальня (пом. 2)

Стадия	Лист	Листов
П	58	105


выпуск 14.11.2026 № 3aed0ef730 · стр. 58 из 105

Стена Б (М 1:20)

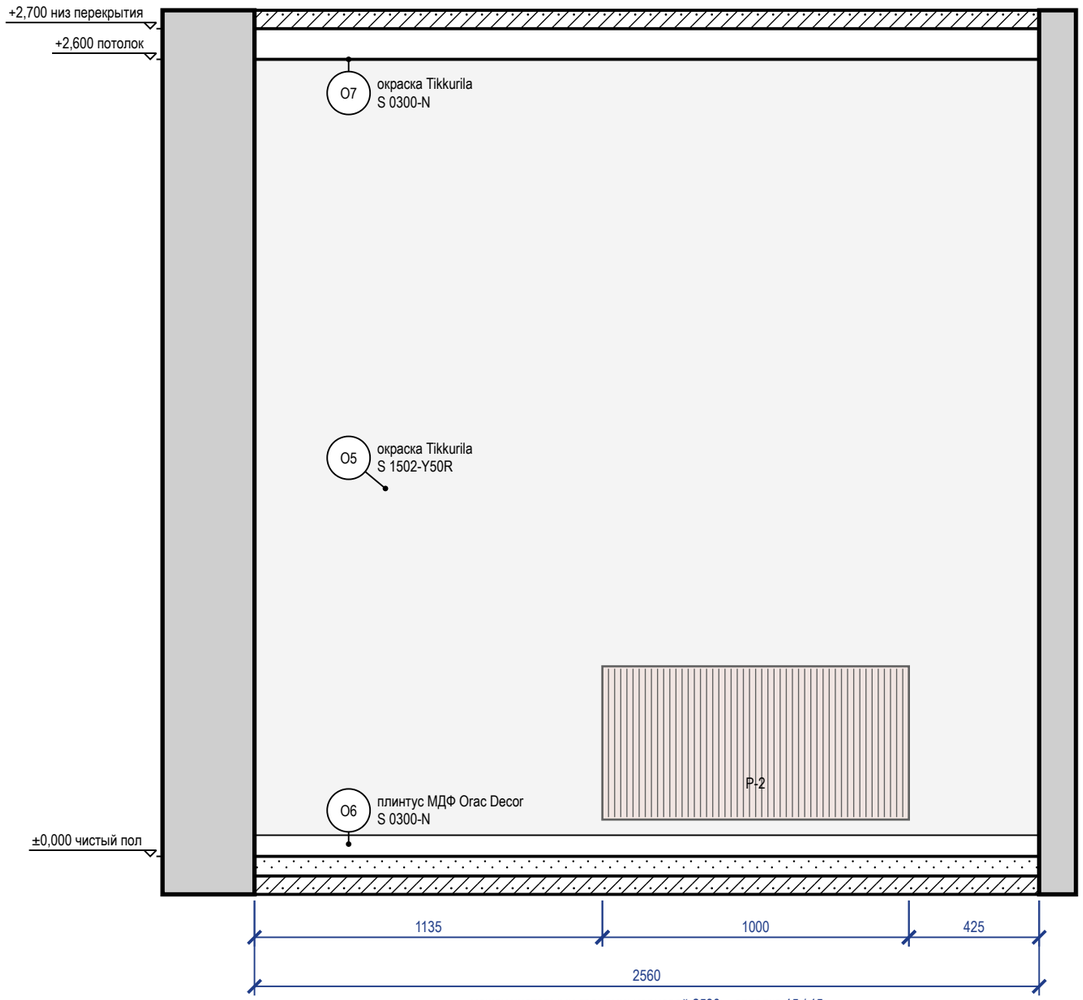

между чистовыми гранями: черновой 2590 − отделка 15 / 15

Стена Г (М 1:20)

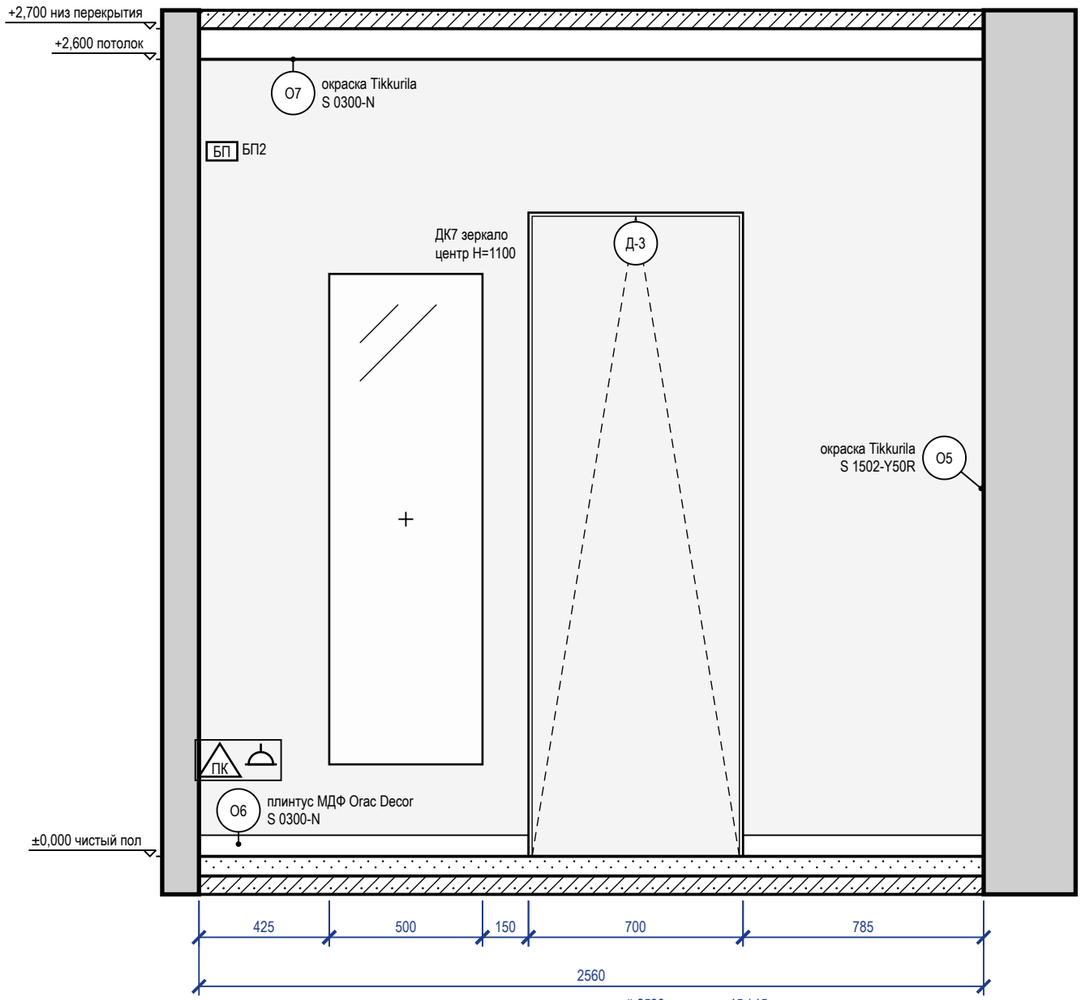

между чистовыми гранями: черновой 2590 − отделка 15 / 15


Ведомость точек и выводов

Стена	Марка	Что это	Гр.	Н, мм	От угла, мм	Примечание
Г	LAN2	розетка RJ45: рабочее место, ТВ		300	75	
Г	БП2	блок питания LED	1	2300	75	
Г	Р3	розетка: комод, зарядка	4	300	175	

Ведомость отделки (на листе)

Марка	Поверхность	Материал, изделие	Цвет, код	Кол.
О5	стены	окраска, Tikkurila, глубокоматовая, подготовка Q3	NCS S 1502-Y50R	11,8 м²
О6	плинтус	плинтус МДФ, Orac Decor Contour (Luxxus), h 69 мм, SX165, шелковисто-матовая	NCS S 0300-N	4,4 м
О7	потолок	окраска, Tikkurila, глубокоматовая	NCS S 0300-N	8,3 м²

Схема развёрток (М 1:100)

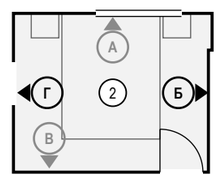


Примечания

1. Размеры — в мм от чистовых поверхностей стен; условные обозначения и общие указания — лист 14.
2. Картины и зеркала крепить к основанию по паспорту изделия (закладные и анкеры — в перечне скрытых работ); крест — ось центра предмета.
3. Двери скрытого монтажа — полотно в плоскости стены, отделка стены по полотну, плинтус прерывается у короба (узел — на листе узлов).
4. Часть марок не уместилась у знаков: коды, высоты и привязки этих позиций — в ведомости точек и выводов под видами.

	Лист	№ док.	Подпись	Дата	Проект: Квартира 65 м²			М 1:20
Дизайнер	Кырлан А.С.			14.11.26	Развёртки стен Б, Г. Спальня (пом. 2)	Стадия	Лист	Листов
Проверил						П	59	105
Н. контр.								
Утв.								


выпуск 14.11.2026 № 3aed0ef730 · стр. 59 из 105

Стена В (М 1:20)

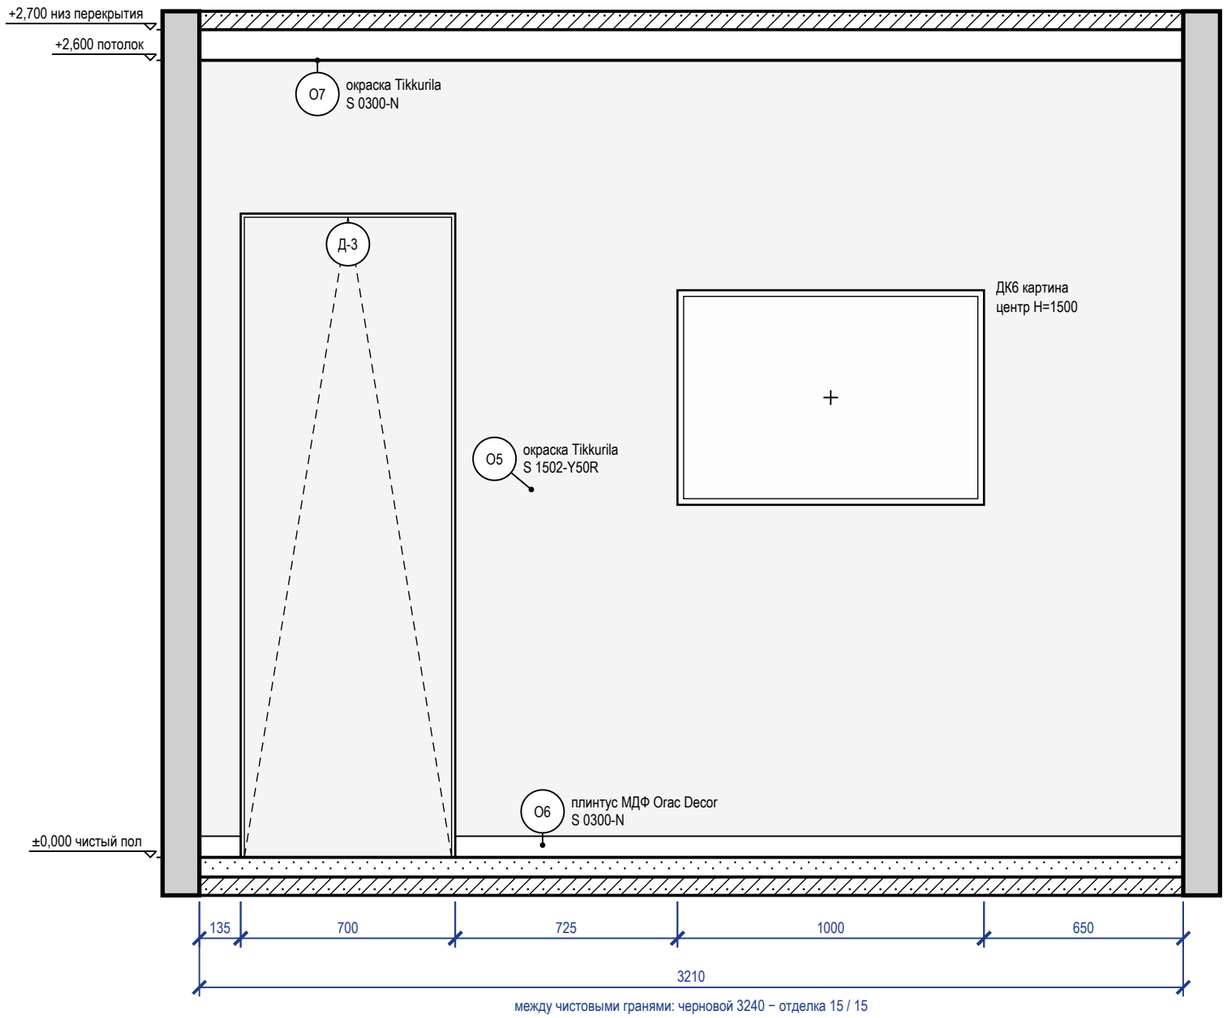

между чистовыми гранями: черновой 3240 − отделка 15 / 15

Схема развёрток (М 1:50)

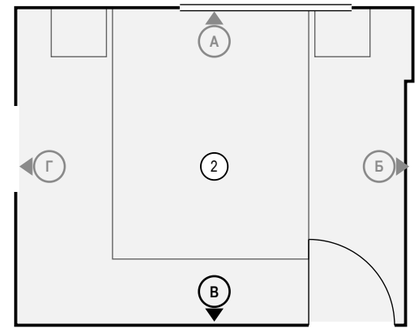


Ведомость отделки (на листе)

Марка	Поверхность	Материал, изделие	Цвет, код	Кол.
О5	стены	окраска, Tikkurila, глубокоматовая, подготовка Q3	NCS S 1502-Y50R	6,9 м²
О6	плинтус	плинтус МДФ, Orac Decor Contour (Luxxus), h 69 мм, SX165, шелковисто-матовая	NCS S 0300-N	2,5 м
О7	потолок	окраска, Tikkurila, глубокоматовая	NCS S 0300-N	8,3 м²

Ведомость изделий и проёмов (на листе)

Марка	Изделие, проём	На виде Ш×В, мм	Низ, мм
Д-3	дверь скрытого монтажа	700×2100	0
ДК6	картина	1000×700	1150

2 **Дверь скрытого монтажа в плоскости стены, плинтус (М 1:5)**
Узел 2 — лист С13

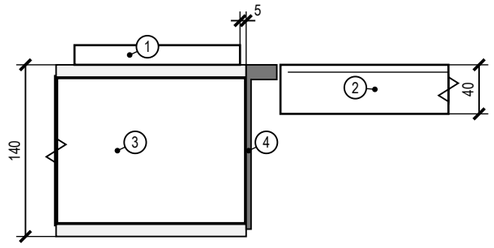

Поз.	Состав слоя, изделие
1	плинтус МДФ 69×16 на клей; у короба — зазор 5 мм, окраска в цвет стены
2	полотно 40 мм под окраску, заподлицо со стеной; теневой шов 3 мм
3	стена 120 мм, штукатурка 10 мм с двух сторон
4	короб скрытого монтажа (алюминий), лицом в плоскости отделки; монтаж до штукатурки


Примечания

1. Размеры — в мм от чистовых поверхностей стен; условные обозначения и общие указания — лист 14.
2. Картины и зеркала крепить к основанию по паспорту изделия (закладные и анкеры — в перечне скрытых работ); крест — ось центра предмета.
3. Двери скрытого монтажа — полотно в плоскости стены, отделка стены по полотну, плинтус прерывается у короба (узел — на листе узлов).

	Лист	№ док.	Подпись	Дата	Проект: Квартира 65 м²			М 1:20
Дизайнер	Кырлан А.С.			14.11.26	Развёртка стены В. Спальня (пом. 2)	Стадия	Лист	Листов
Проверил						П	60	105
Н. контр.								
Утв.								


выпуск 14.11.2026 № 3aed0ef730 · стр. 60 из 105

Стена В2 (М 1:20)

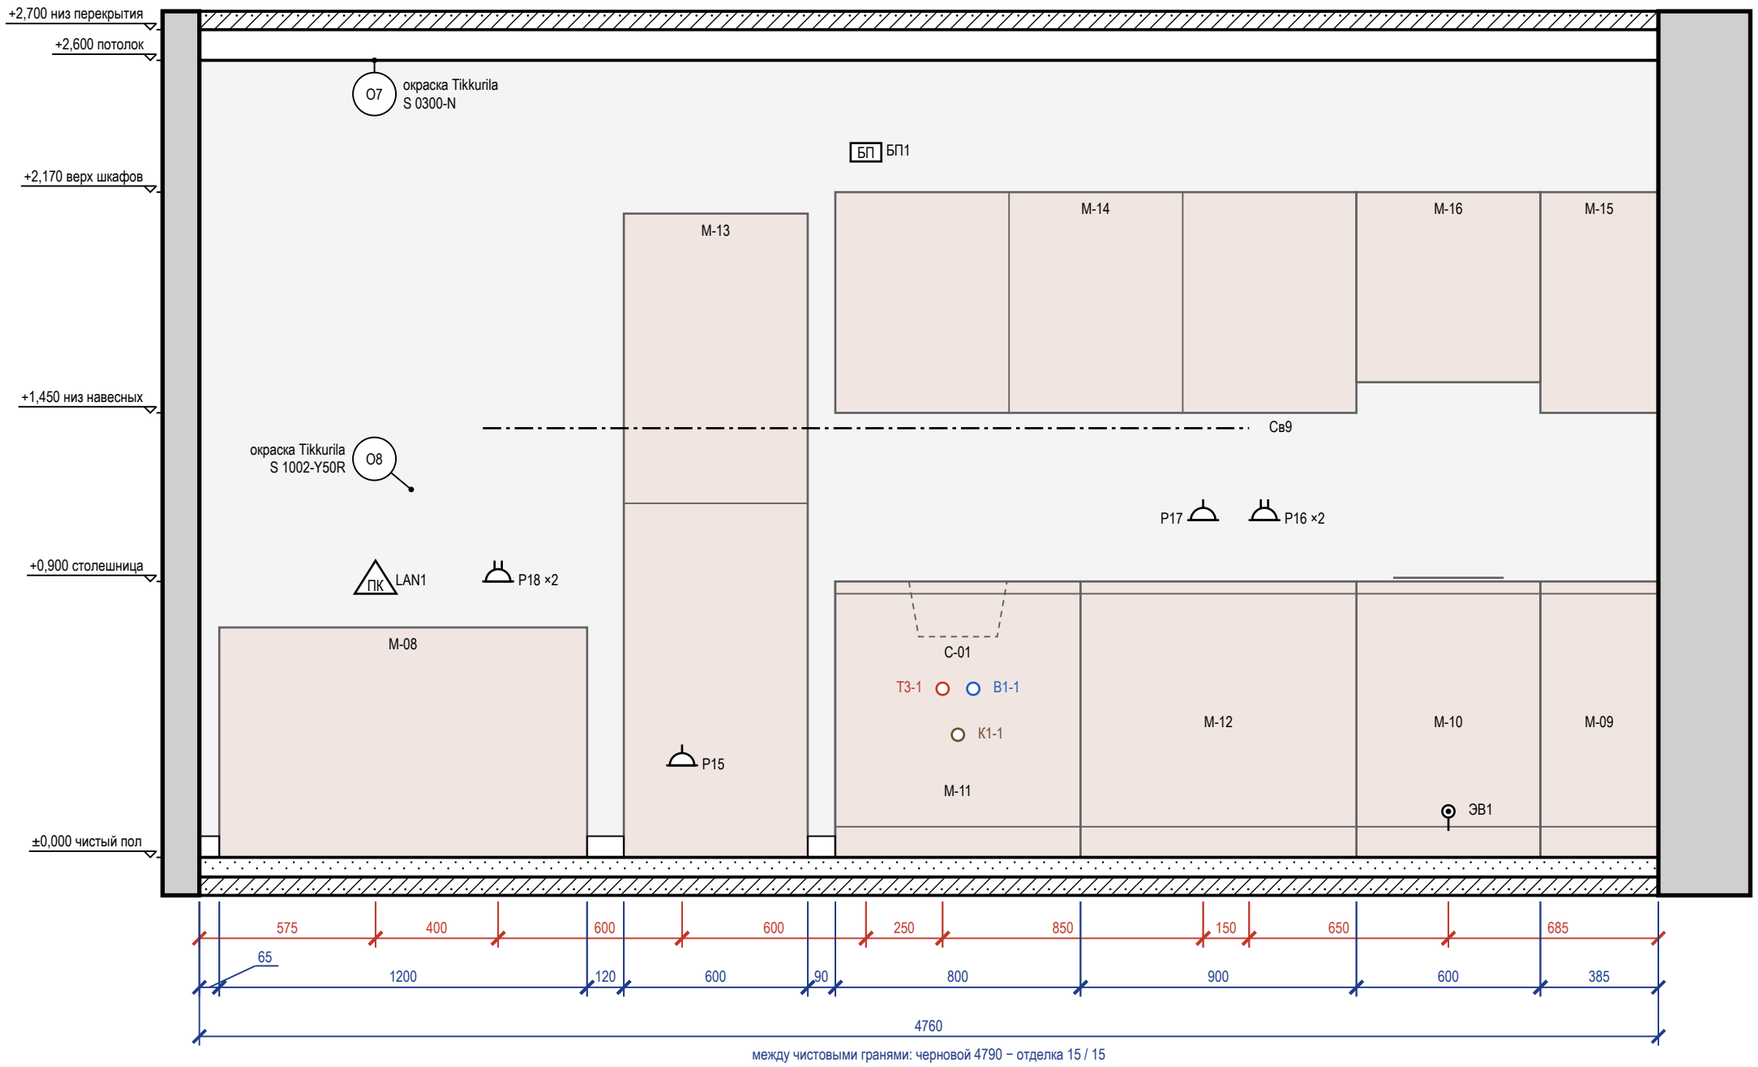

между чистовыми гранями: черновой 4790 − отделка 15 / 15

Схема развёрток (М 1:100)

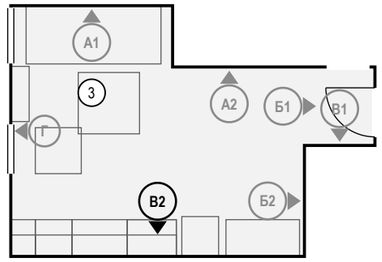

Ведомость точек и выводов

Марка	Что это	Гр.	Н, мм	От угла, мм	Примечание
LAN1	розетка RJ45: рабочее место		900	575	
Р18	розетка: рабочее место	4	900	975	рамка 2 поста
Р15	розетка: холодильник	2	300	1575	
БП1	блок питания LED	1	2300	2175	
Т3-1	горячая вода — мойка кухонная		550	2425	межос. 100
К1-1	канализация — мойка кухонная		400	2475	Ø50

Марка	Что это	Гр.	Н, мм	От угла, мм	Примечание
В1-1	холодная вода — мойка кухонная		550	2525	межос. 100
Р17	розетка: рабочая зона	2	1100	3275	
Св9	светильник настенный	1	1400	3425	лента 925–3425 от угла
Р16	розетка: рабочая зона	2	1100	3475	рамка 2 поста
ЭВ1	вывод кабеля: варочная панель	3	150	4075	

Ведомость отделки (на листе)

Марка	Поверхность	Материал, изделие	Цвет, код	Кол.
О6	плинтус	плинтус МДФ, Orac Decor Contour (Luxxus), h 69 мм, SX165, шелковисто-матовая	NCS S 0300-N	0,3 м
О7	потолок	окраска, Tikkurila, глубокоматовая	NCS S 0300-N	18,9 м²
О8	стены	окраска, Tikkurila, шелковисто-матовая, подготовка Q3	NCS S 1002-Y50R	12,4 м²

Примечания

1. Размеры — в мм от чистовых поверхностей стен; условные обозначения и общие указания — лист 14.
2. Выводы кухонной техники — по утверждённому проекту кухни: привязки выводов даются от осей модулей гарнитура.

	Лист	№ док.	Подпись	Дата
Дизайнер	Кырлан А.С.			14.11.26
Проверил				
Н. контр.				
Утв.				


Проект: Квартира 65 м² — М 1:20

Развёртка стены В2. Кухня-гостиная (пом. 3), кухонный фронт

Стадия	Лист	Листов
П	61	105

выпуск 14.11.2026 № 3aed0ef730 · стр. 61 из 105


Стена Г (М 1:20)

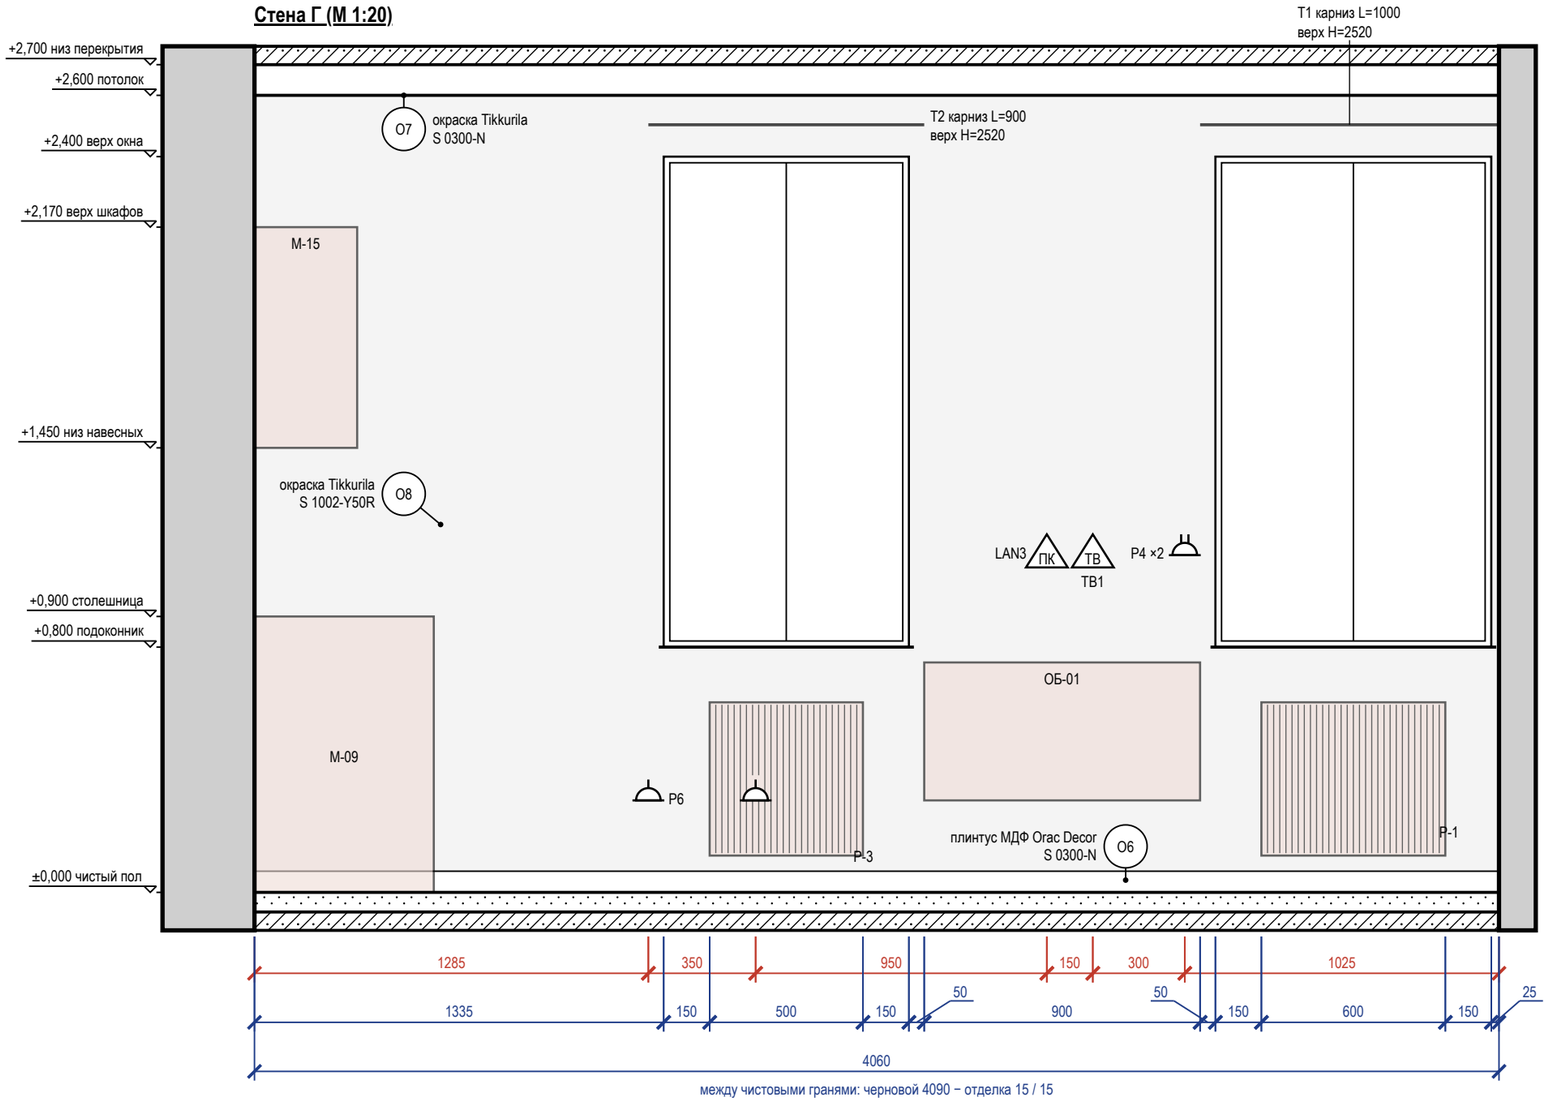

Ведомость отделки (на листе)

Марка	Поверхность	Материал, изделие	Цвет, код	Кол.
О6	плинтус	плинтус МДФ, Orac Decor Contour (Luxxus), h 69 мм, SX165, шелковисто-матовая	NCS S 0300-N	4,1 м
О7	потолок	окраска, Tikkurila, глубокоматовая	NCS S 0300-N	18,9 м²
О8	стены	окраска, Tikkurila, шелковисто-матовая, подготовка Q3	NCS S 1002-Y50R	7,8 м²

Схема развёрток (М 1:100)

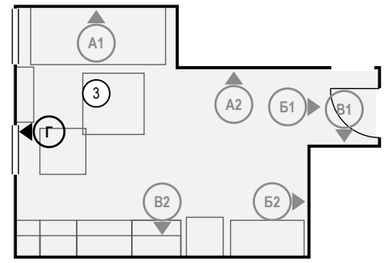

Ведомость точек и выводов

Марка	Что это	Гр.	Н, мм	От угла, мм	Примечание
Р6	розетка: торшер у кресла М-06	4	300	1285	
Р5	розетка: обеденная зона	4	300	1635	
LAN3	розетка RJ45: Smart TV		1100	2585	
ТВ1	розетка ТВ: ТВ на стене		1100	2735	
Р4	розетка: ТВ, приставка	4	1100	3035	рамка 2 поста

Ведомость изделий и проёмов (на листе)

Марка	Изделие, проём	На виде Ш×В, мм	Низ, мм
М-09	модуль нижний	585×900	0
М-15	навесной модуль	335×720	1450
Р-3	радиатор отопления	500×500	120
ОБ-01	ТВ на стене, тумба подвесная	900×450	300
Р-1	радиатор отопления	600×500	120

Примечания

1. Размеры — в мм от чистовых поверхностей стен; условные обозначения и общие указания — лист 14.
2. Карнизы (шины) — по ведомости текстиля декоратора: длина L и верх H на развёртке — те же числа, что в ведомости; крепление — до окраски потолка.
3. Выводы кухонной техники — по утверждённому проекту кухни: привязки выводов даются от осей модулей гарнитура.
4. Карниз T1: по ведомости текстиля шина L=1000 мм, а от её начала до чистового угла стены — 975 мм: шина не встаёт, длину согласовать с декоратором до заказа.
5. Линии узора (швы плитки, складки штор, рёбра радиаторов) прерываются у знаков и выносок — просвет между линиями не менее 0,7 мм.
6. Часть марок не уместилась у знаков: коды, высоты и привязки этих позиций — в ведомости точек и выводов под видами.

	Лист	№ док.	Подпись	Дата
Дизайнер	Кырлан А.С.			14.11.26
Проверил				
Н. контр.				
Утв.				


Проект: Квартира 65 м² — **М 1:20**

Развёртка стены Г. Кухня-гостиная (пом. 3), кухонный фронт

Стадия	Лист	Листов
П	62	105

выпуск 14.11.2026 № 3aed0ef730 · стр. 62 из 105

Стена А1 (М 1:20)

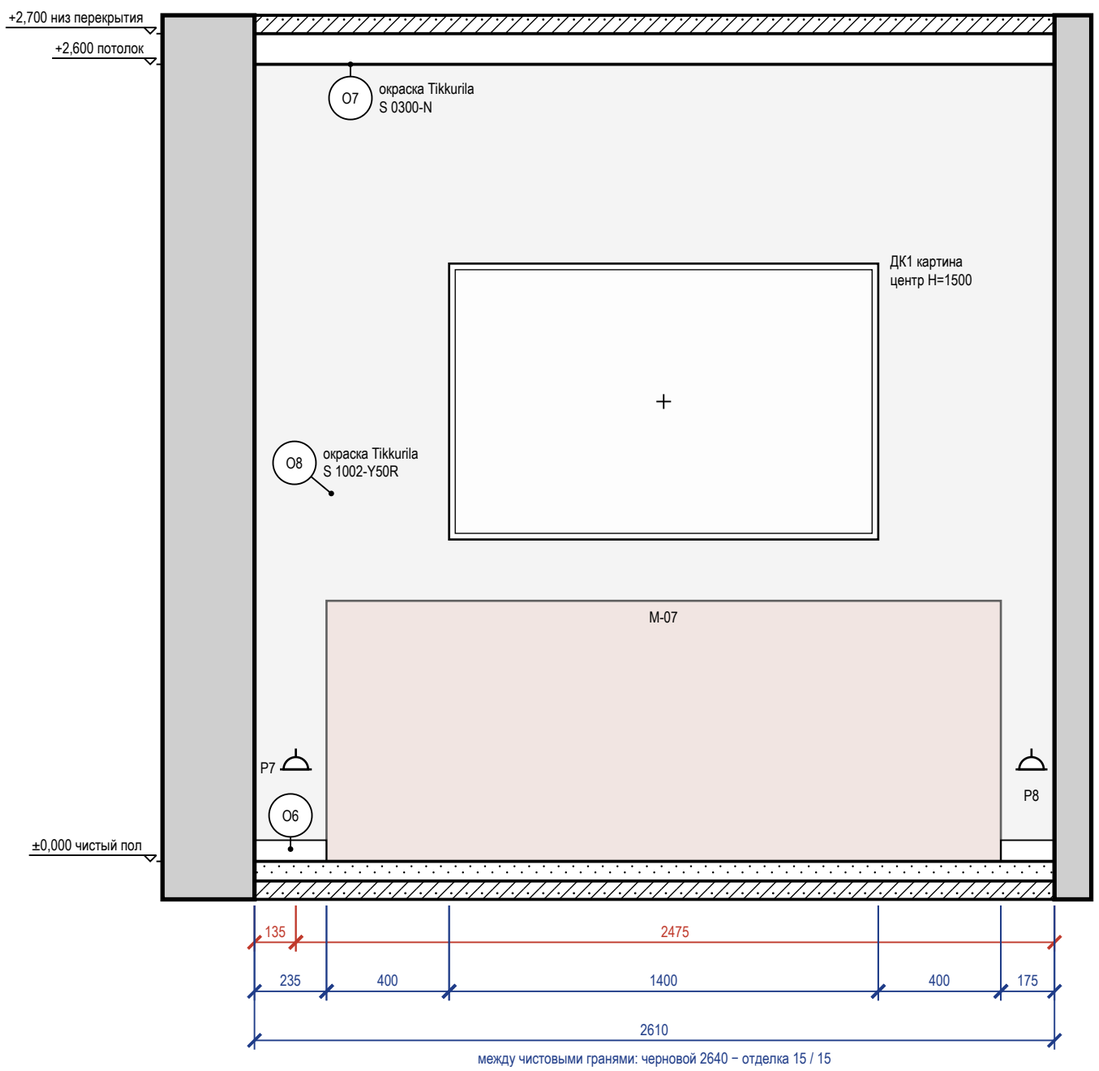


Стена А1 — визуализация, лист 6



Ведомость отделки (на листе)

Марка	Поверхность	Материал, изделие	Цвет, код	Кол.
О6	плинтус	плинтус МДФ, Orac Decor Contour (Luxxus), h 69 мм, SX165, шелковисто-матовая	NCS S 0300-N	0,4 м
О7	потолок	окраска, Tikkurila, глубокоматовая	NCS S 0300-N	18,9 м²
О8	стены	окраска, Tikkurila, шелковисто-матовая, подготовка Q3	NCS S 1002-Y50R	6,8 м²

Схема развёрток (М 1:50)

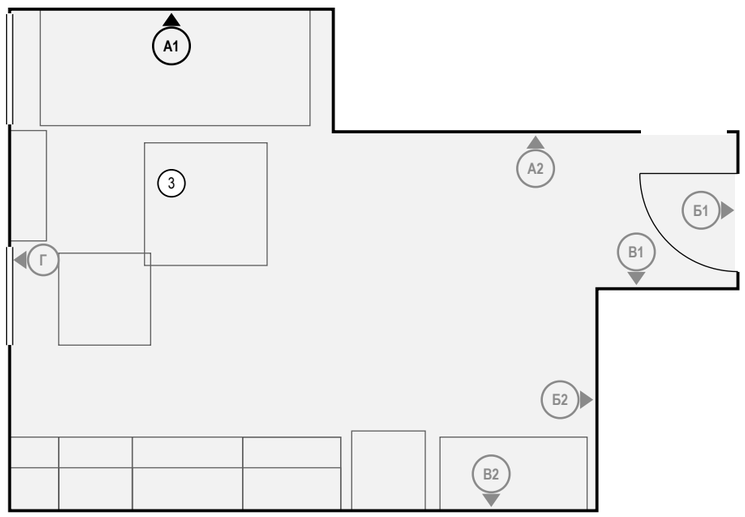

Ведомость точек и выводов

Марка	Что это	Гр.	Н, мм	От угла, мм	Примечание
Р7	розетка: у дивана	4	300	135	
Р8	розетка: у дивана	4	300	2535	

Ведомость изделий и проёмов (на листе)

Марка	Изделие, проём	На виде Ш×В, мм	Низ, мм
М-07	диван	2200×850	0
ДК1	картина	1400×900	1050

Примечания

1. Размеры — в мм от чистовых поверхностей стен; условные обозначения и общие указания — лист 14.
2. Картины и зеркала крепить к основанию по паспорту изделия (закладные и анкеры — в перечне скрытых работ); крест — ось центра предмета.

	Лист	№ док.	Подпись	Дата
Дизайнер	Кырлан А.С.			14.11.26
Проверил				
Н. контр.				
Утв.				

Проект: Квартира 65 м² — **М 1:20**

Развёртка стены А1. Кухня-гостиная (пом. 3)

Стадия	Лист	Листов
П	63	105

выпуск 14.11.2026 № 3aed0ef730 · стр. 63 из 105

Стена А2 (М 1:20)



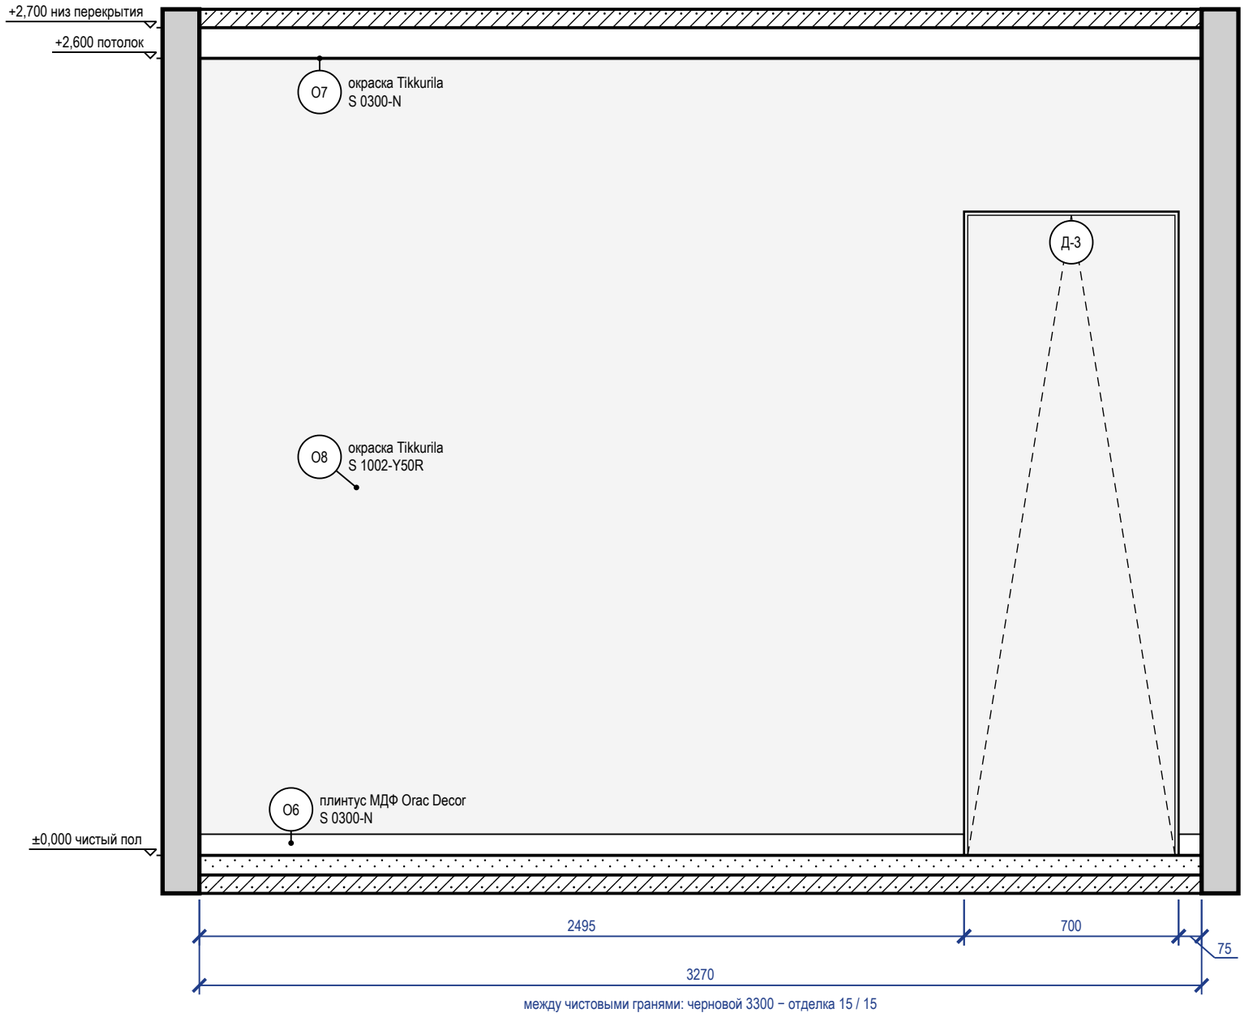


Схема развёрток (М 1:50)

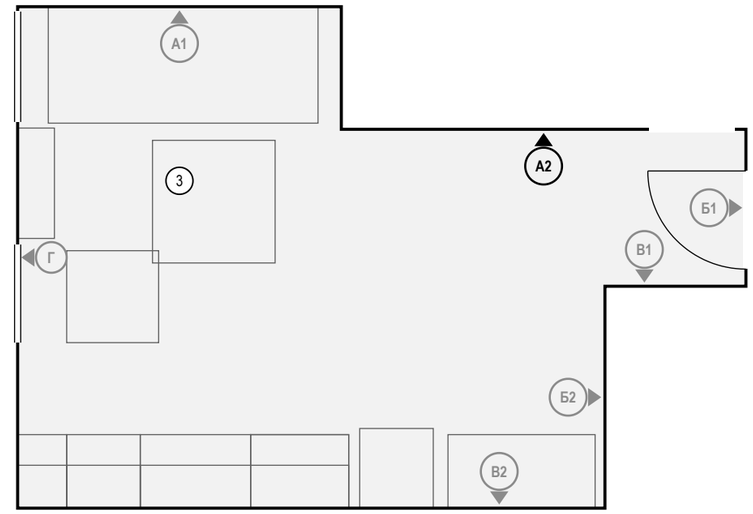

5 **Плинтус МДФ 69×16 мм у окрашенной стены по доске (ламинату) (М 1:10)**
Узел 5 — лист С13

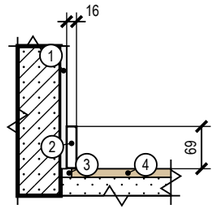

Поз.	Состав слоя, изделие
1	штукатурка, шпаклёвка Q3, окраска — по ведомости отделки
2	плинтус МДФ 69×16 под окраску в цвет стены; клей монтажный — к стене, не к полу
3	зазор покрытия у стены 8–10 мм закрывается плинтусом
4	инженерная доска на клею


Ведомость отделки (на листе)

Марка	Поверхность	Материал, изделие	Цвет, код	Кол.
О6	плинтус	плинтус МДФ, Orac Decor Contour (Luxxus), h 69 мм, SX165, шелковисто-матовая	NCS S 0300-N	2,6 м
О7	потолок	окраска, Tikkurila, глубокоматовая	NCS S 0300-N	18,9 м²
О8	стены	окраска, Tikkurila, шелковисто-матовая, подготовка Q3	NCS S 1002-Y50R	7 м²

Ведомость изделий и проёмов (на листе)

Марка	Изделие, проём	На виде Ш×В, мм	Низ, мм
Д-3	дверь скрытого монтажа	700×2100	0

2 **Дверь скрытого монтажа в плоскости стены, плинтус (М 1:5)**
Узел 2 — лист С13

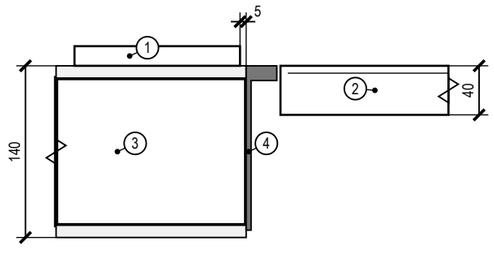

Поз.	Состав слоя, изделие
1	плинтус МДФ 69×16 на клей; у короба — зазор 5 мм, окраска в цвет стены
2	полотно 40 мм под окраску, заподлицо со стеной; теневой шов 3 мм
3	стена 120 мм, штукатурка 10 мм с двух сторон
4	короб скрытого монтажа (алюминий), лицом в плоскости отделки; монтаж до штукатурки


Примечания

1. Размеры — в мм от чистовых поверхностей стен; условные обозначения и общие указания — лист 14.
2. Двери скрытого монтажа — полотно в плоскости стены, отделка стены по полотну, плинтус прерывается у короба (узел — на листе узлов).

	Лист	№ док.	Подпись	Дата	Проект: Квартира 65 м²			М 1:20
Дизайнер	Кырлан А.С.			14.11.26	Развёртка стены А2. Кухня-гостиная (пом. 3)	Стадия	Лист	Листов
Проверил						П	64	105
Н. контр.								
Утв.								


выпуск 14.11.2026 № 3aed0ef730 · стр. 64 из 105

Стена Б1 (М 1:20)

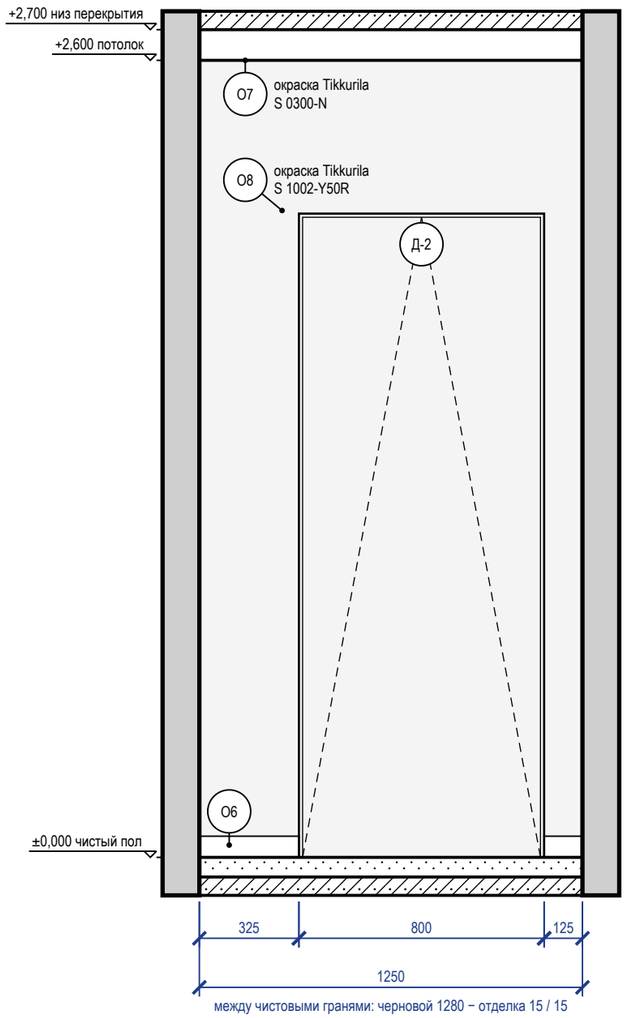


между чистовыми гранями: черновой 1280 − отделка 15 / 15

Стена Б2 (М 1:20)

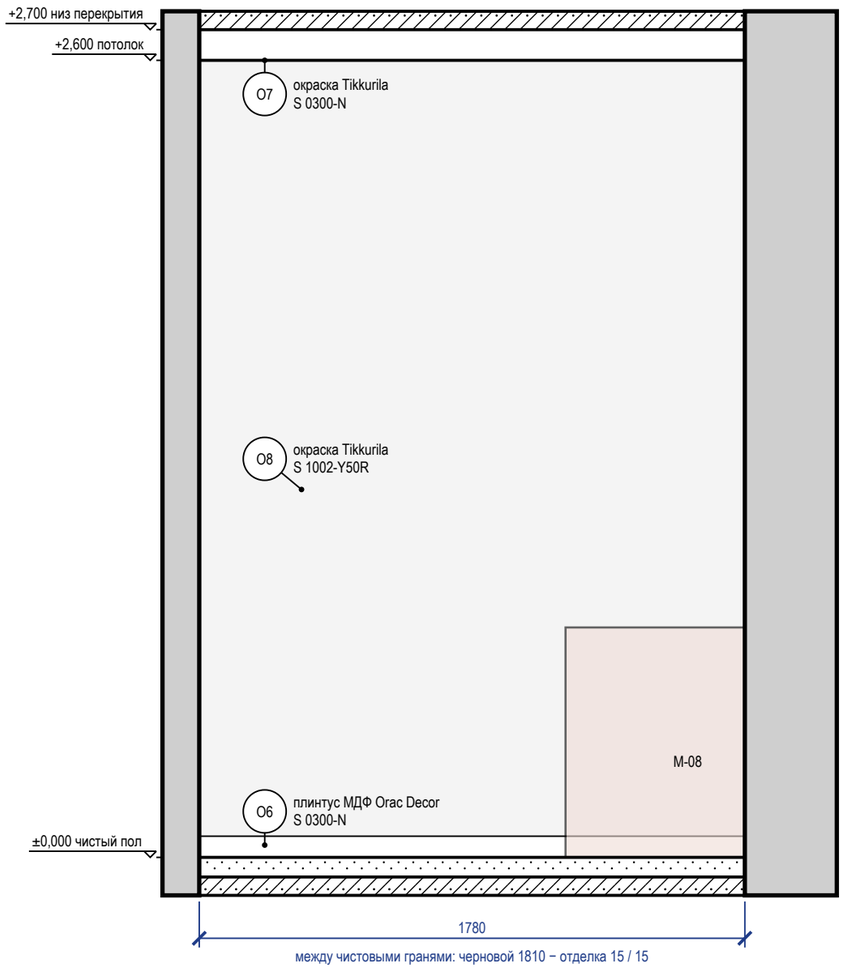

между чистовыми гранями: черновой 1810 − отделка 15 / 15

Стена В1 (М 1:20)

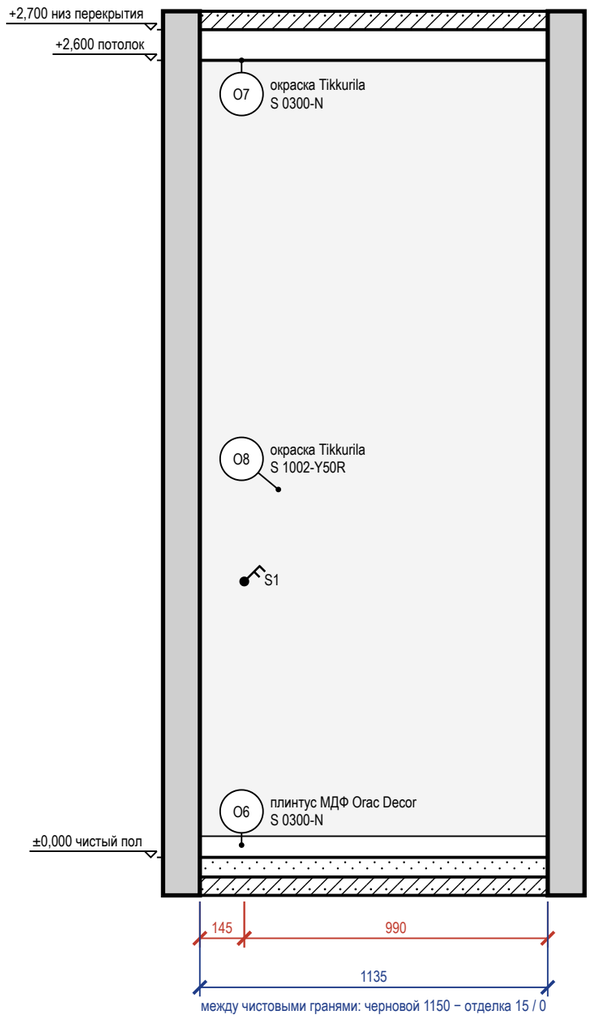

между чистовыми гранями: черновой 1150 − отделка 15 / 0

Ведомость точек и выводов

Стена	Марка	Что это	Гр.	Н, мм	От угла, мм	Примечание
В1	S1	выключатель	1	900	145	


Ведомость изделий и проёмов (на листе)

Стена	Марка	Изделие, проём	На виде Ш×В, мм	Низ, мм
Б1	Д-2	дверь скрытого монтажа	800×2100	0
Б2	М-08	стол рабочий (кабинет)	585×750	0

Ведомость отделки (на листе)

Марка	Поверхность	Материал, изделие	Цвет, код	Кол.
О6	плинтус	плинтус МДФ, Orac Decor Contour (Luxxus), h 69 мм, SX165, шелковисто-матовая	NCS S 0300-N	3,4 м
О7	потолок	окраска, Tikkurila, глубокоматовая	NCS S 0300-N	18,9 м²
О8	стены	окраска, Tikkurila, шелковисто-матовая, подготовка Q3	NCS S 1002-Y50R	9,1 м²

Схема развёрток (М 1:100)

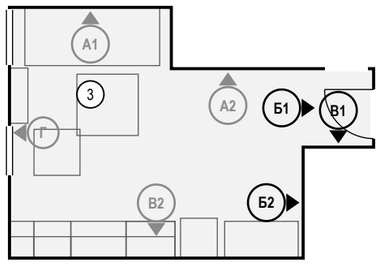


Примечания

1. Размеры — в мм от чистовых поверхностей стен; условные обозначения и общие указания — лист 14.
2. Двери скрытого монтажа — полотно в плоскости стены, отделка стены по полотну, плинтус прерывается у короба (узел — на листе узлов).

	Лист	№ док.	Подпись	Дата	Проект: Квартира 65 м²	М 1:20		
Дизайнер	Кырлан А.С.			14.11.26	Развёртки стен Б1, Б2, В1. Кухня-гостиная (пом. 3)	Стадия	Лист	Листов
Проверил						П	65	105
Н. контр.								
Утв.								


выпуск 14.11.2026 № 3aed0ef730 · стр. 65 из 105

Стена А (М 1:20)

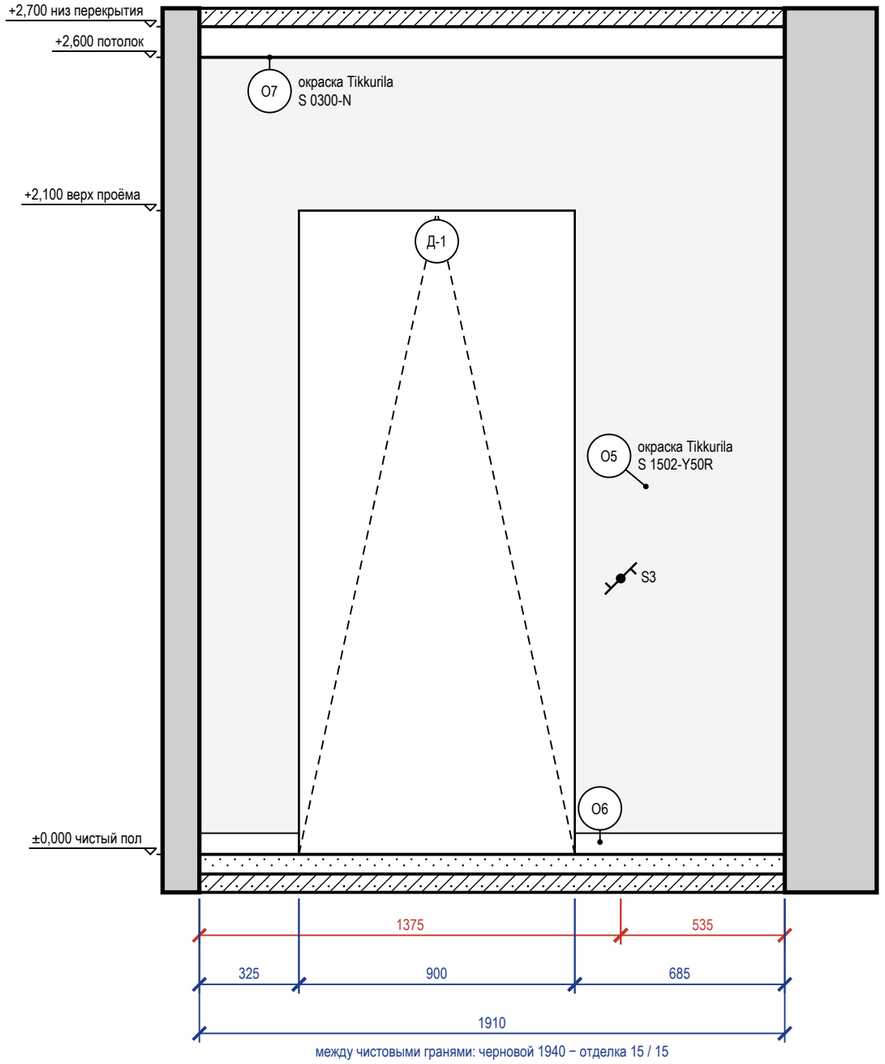

между чистовыми гранями: черновой 1940 − отделка 15 / 15

Стена Б (М 1:20)

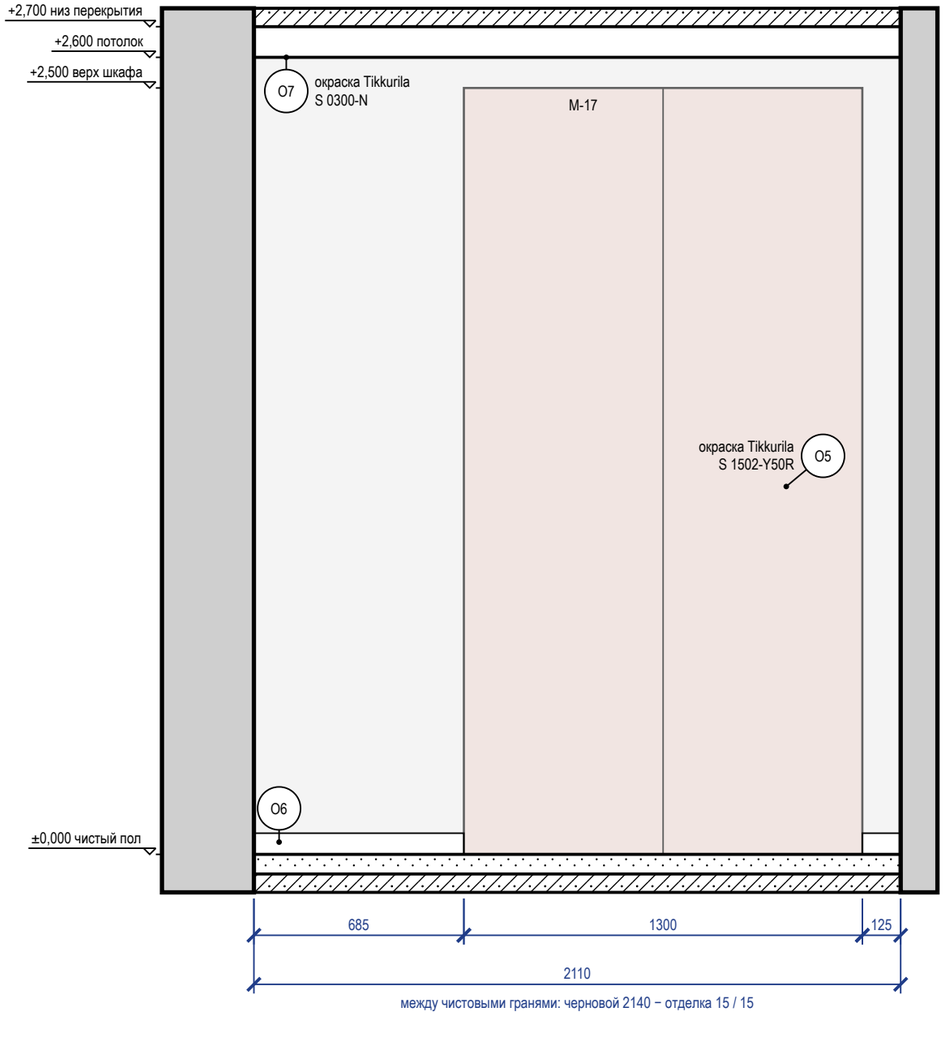

между чистовыми гранями: черновой 2140 − отделка 15 / 15

Ведомость точек и выводов

Стена	Марка	Что это	Гр.	Н, мм	От угла, мм	Примечание
А	S3	выключатель	1	900	1375	


Ведомость изделий и проёмов (на листе)

Стена	Марка	Изделие, проём	На виде Ш×В, мм	Низ, мм
А	Д-1	дверь	900×2100	0
Б	М-17	шкаф-купе	1300×2500	0

Ведомость отделки (на листе)

Марка	Поверхность	Материал, изделие	Цвет, код	Кол.
О5	стены	окраска, Tikkurila, шелковисто-матовая, подготовка Q3	NCS S 1502-Y50R	8,6 м²
О6	плинтус	плинтус МДФ, Orac Decor Contour (Luxxus), h 69 мм, SX165, шелковисто-матовая	NCS S 0300-N	1,8 м
О7	потолок	окраска, Tikkurila, глубокоматовая	NCS S 0300-N	4,2 м²

Схема развёрток (М 1:50)

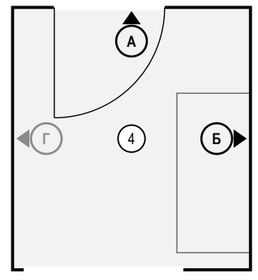


Примечания

1. Размеры — в мм от чистовых поверхностей стен; условные обозначения и общие указания — лист 14.

	Лист	№ док.	Подпись	Дата	Проект: Квартира 65 м²	М 1:20		
Дизайнер	Кырлан А.С.			14.11.26	Развёртки стен А, Б. Прихожая (пом. 4)	Стадия	Лист	Листов
Проверил						П	66	105
Н. контр.								
Утв.								


выпуск 14.11.2026 № 3aed0ef730 · стр. 66 из 105

Стена Г (М 1:20)

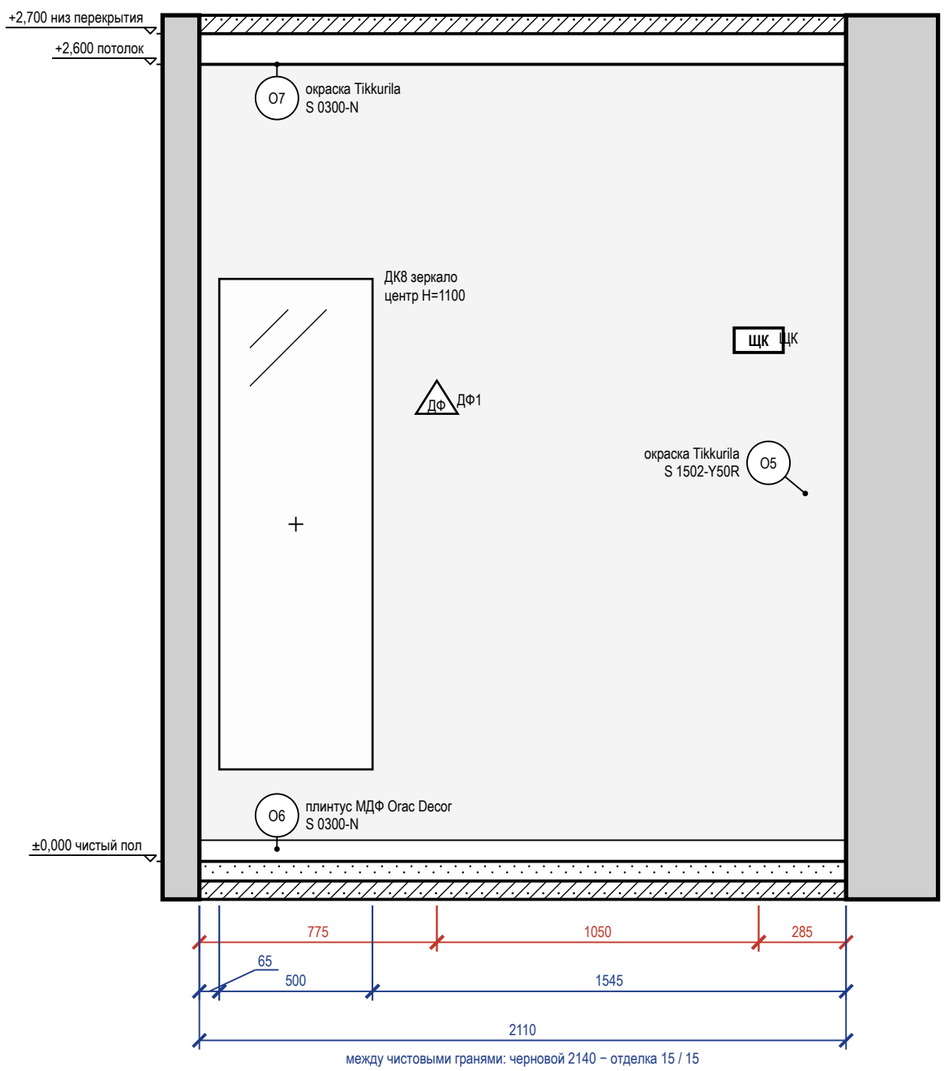

6 Плинтус МДФ 69×16 мм у окрашенной стены по керамограниту (плитке) (М 1:5)

Узел 6 — лист С13

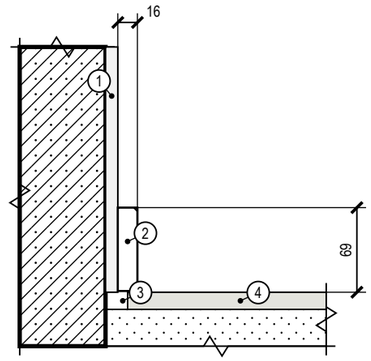

Поз.	Состав слоя, изделие
1	штукатурка, шпаклёвка Q3, окраска — по ведомости отделки
2	плинтус МДФ 69×16 под окраску в цвет стены; клей монтажный — к стене, не к полу
3	зазор покрытия у стены 8–10 мм закрывается плинтусом
4	керамогранит на клею C2 TE S1

Ведомость точек и выводов

Марка	Что это	Гр.	H, мм	От угла, мм	Примечание
ДФ1	домофон: трубка домофона		1500	775	
ЩК	щит		1700	1825	


Ведомость изделий и проёмов (на листе)

Марка	Изделие, проём	На виде Ш×В, мм	Низ, мм
ДК8	зеркало	500×1600	300

Ведомость отделки (на листе)

Марка	Поверхность	Материал, изделие	Цвет, код	Кол.
О5	стены	окраска, Tikkurila, шелковисто-матовая, подготовка Q3	NCS S 1502-Y50R	5,5 м²
О6	плинтус	плинтус МДФ, Orac Decor Contour (Luxxus), h 69 мм, SX165, шелковисто-матовая	NCS S 0300-N	2,1 м
О7	потолок	окраска, Tikkurila, глубокоматовая	NCS S 0300-N	4,2 м²

Схема развёрток (М 1:50)

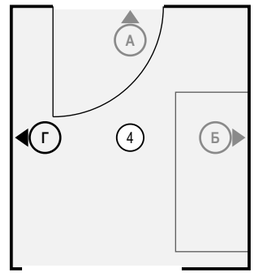


Примечания

1. Размеры — в мм от чистовых поверхностей стен; условные обозначения и общие указания — лист 14.
2. Картины и зеркала крепить к основанию по паспорту изделия (закладные и анкеры — в перечне скрытых работ); крест — ось центра предмета.

	Лист	№ док.	Подпись	Дата	Проект: Квартира 65 м²	М 1:20		
Дизайнер	Кырлан А.С.			14.11.26	Развёртка стены Г. Прихожая (пом. 4)	Стадия	Лист	Листов
Проверил						П	67	105
Н. контр.								
Утв.								


выпуск 14.11.2026 № 3aed0ef730 · стр. 67 из 105

Стена А (М 1:20)

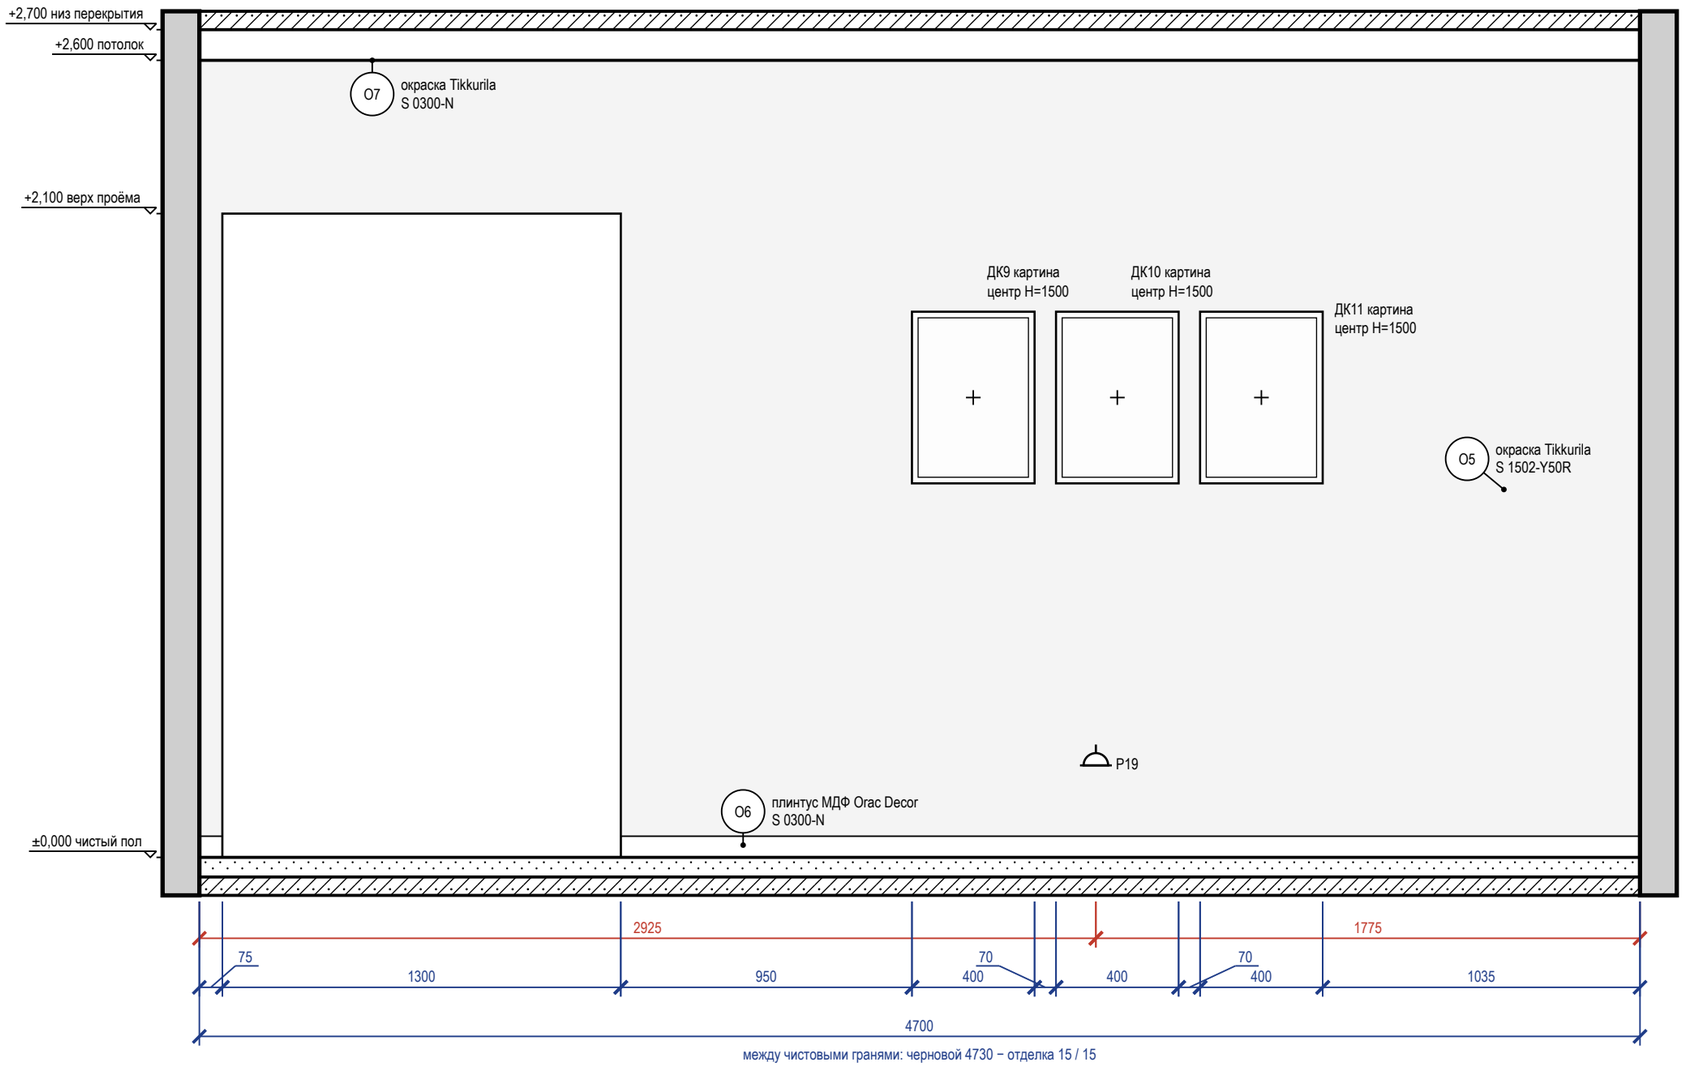

между чистовыми гранями: черновой 4730 − отделка 15 / 15

Стена А — визуализация, лист 8

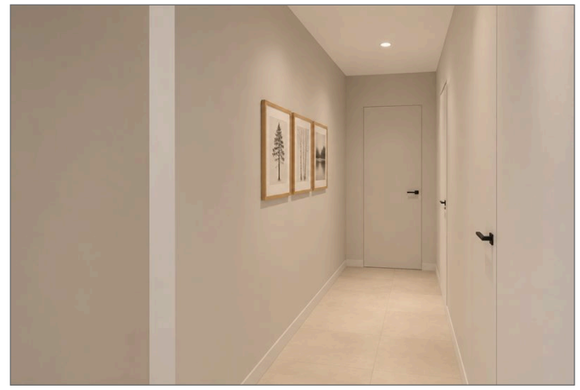

Ведомость точек и выводов

Марка	Что это	Гр.	H, мм	От угла, мм	Примечание
Р19	розетка: уборка	4	300	2925	


Ведомость изделий и проёмов (на листе)

Марка	Изделие, проём	На виде Ш×В, мм	Низ, мм
ДК9	картина	400×560	1220
ДК10	картина	400×560	1220
ДК11	картина	400×560	1220

Ведомость отделки (на листе)

Марка	Поверхность	Материал, изделие	Цвет, код	Кол.
О5	стены	окраска, Tikkurila, шелковисто-матовая, подготовка Q3	NCS S 1502-Y50R	9,5 м²
О6	плинтус	плинтус МДФ, Orac Decor Contour (Luxxus), h 69 мм, SX165, шелковисто-матовая	NCS S 0300-N	3,4 м
О7	потолок	окраска, Tikkurila, глубокоматовая	NCS S 0300-N	5,5 м²

Схема развёрток (М 1:50)

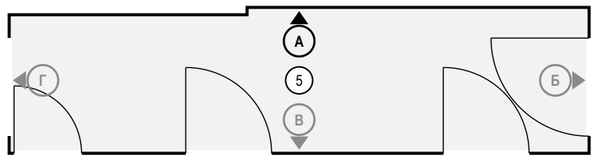

Примечания

1. Размеры — в мм от чистовых поверхностей стен; условные обозначения и общие указания — лист 14.
2. Картины и зеркала крепить к основанию по паспорту изделия (закладные и анкеры — в перечне скрытых работ); крест — ось центра предмета.

	Лист	№ док.	Подпись	Дата
Дизайнер	Кырлан А.С.			14.11.26
Проверил				
Н. контр.				
Утв.				


Проект: Квартира 65 м² — М 1:20

Развёртка стены А. Коридор (пом. 5)


Стадия	Лист	Листов
П	68	105

выпуск 14.11.2026 № 3aed0ef730 · стр. 68 из 105

Стена Б (М 1:20)

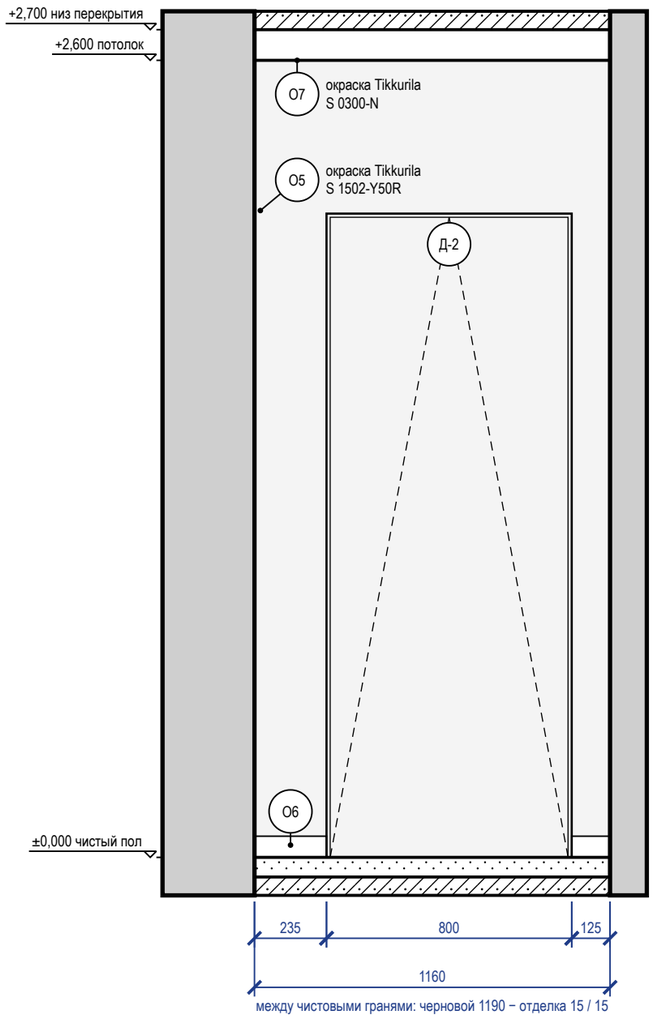


Стена Г (М 1:20)

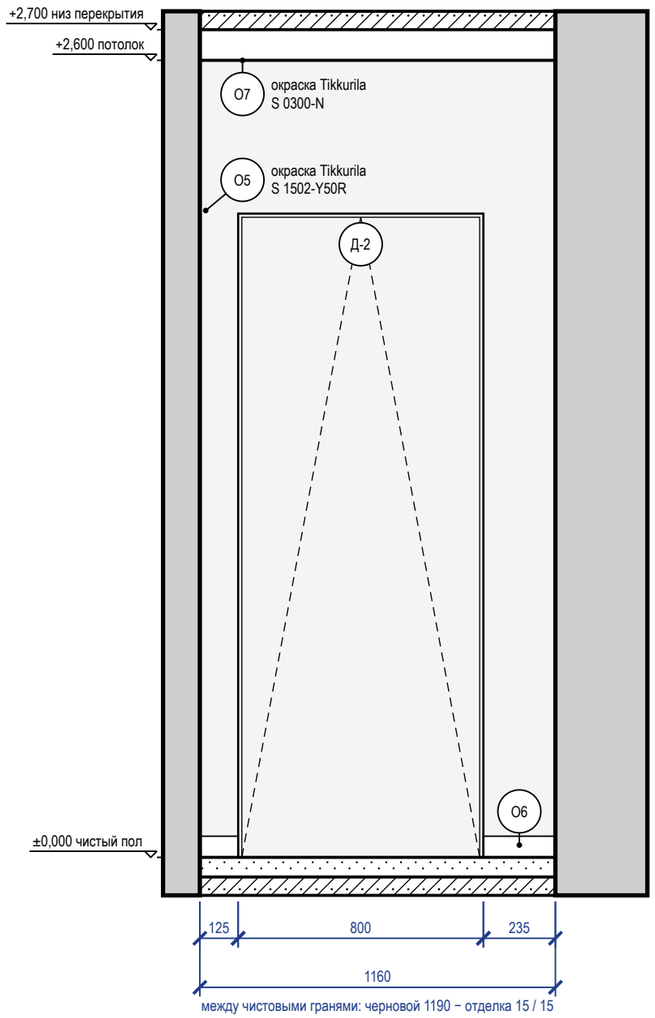

2 Дверь скрытого монтажа в плоскости стены, плинтус (М 1:5)


Узел 2 — лист С13

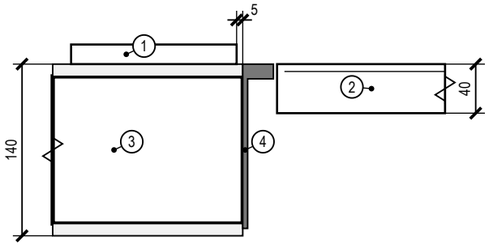

Поз.	Состав слоя, изделие
1	плинтус МДФ 69×16 на клей; у короба — зазор 5 мм, окраска в цвет стены
2	полотно 40 мм под окраску, заподлицо со стеной; теневой шов 3 мм
3	стена 120 мм, штукатурка 10 мм с двух сторон
4	короб скрытого монтажа (алюминий), лицом в плоскости отделки; монтаж до штукатурки

6 Плинтус МДФ 69×16 мм у окрашенной стены по керамограниту (плитке) (М 1:5)

Узел 6 — лист С13

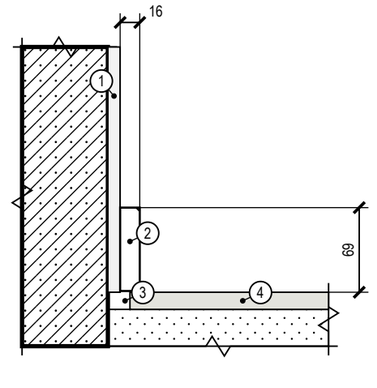


Поз.	Состав слоя, изделие
1	штукатурка, шпаклёвка Q3, окраска — по ведомости отделки
2	плинтус МДФ 69×16 под окраску в цвет стены; клей монтажный — к стене, не к полу
3	зазор покрытия у стены 8–10 мм закрывается плинтусом
4	керамогранит на клею С2 TE S1

Ведомость отделки (на листе)

Марка	Поверхность	Материал, изделие	Цвет, код	Кол.
О5	стены	окраска, Tikkurila, шелковисто-матовая, подготовка Q3	NCS S 1502-Y50R	2,7 м²
О6	плинтус	плинтус МДФ, Orac Decor Contour (Luxxus), h 69 мм, SX165, шелковисто-матовая	NCS S 0300-N	0,7 м
О7	потолок	окраска, Tikkurila, глубокоматовая	NCS S 0300-N	5,5 м²

Схема развёрток (М 1:50)

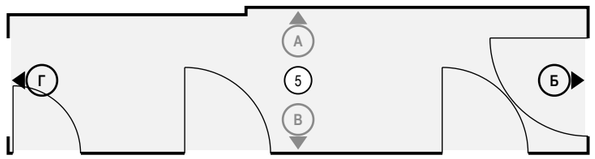

Ведомость изделий и проёмов (на листе)

Стена	Марка	Изделие, проём	На виде Ш×В, мм	Низ, мм
Б	Д-2	дверь скрытого монтажа	800×2100	0
Г	Д-2	дверь скрытого монтажа	800×2100	0

Примечания

1. Размеры — в мм от чистовых поверхностей стен; условные обозначения и общие указания — лист 14.
2. Двери скрытого монтажа — полотно в плоскости стены, отделка стены по полотну, плинтус прерывается у короба (узел — на листе узлов).

	Лист	№ док.	Подпись	Дата
Дизайнер	Кырлан А.С.			14.11.26
Проверил				
Н. контр.				
Утв.				


Проект: Квартира 65 м² — **М 1:20**

Развёртки стен Б, Г. Коридор (пом. 5)

Стадия	Лист	Листов
П	69	105

выпуск 14.11.2026 № 3aed0ef730 · стр. 69 из 105

Стена В (М 1:20)

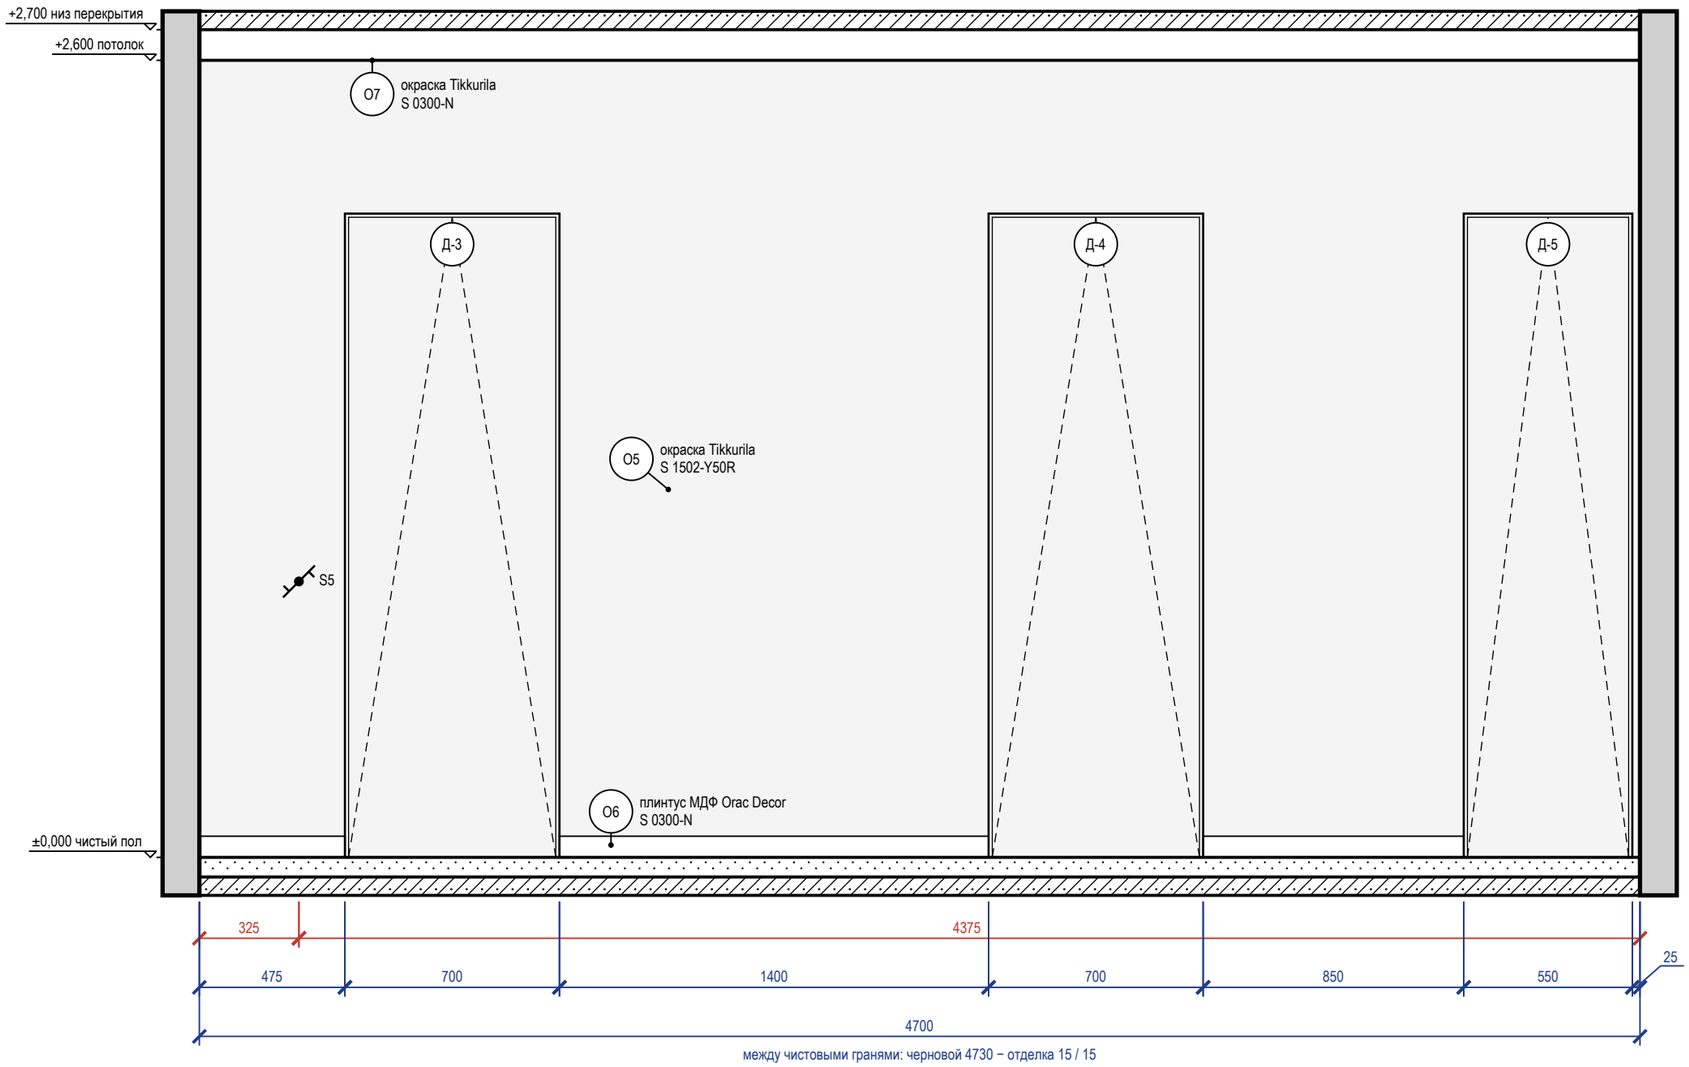

Ведомость точек и выводов

Марка	Что это	Гр.	Н, мм	От угла, мм	Примечание
S5	выключатель	1	900	325	


Ведомость изделий и проёмов (на листе)

Марка	Изделие, проём	На виде Ш×В, мм	Низ, мм
Д-3	дверь скрытого монтажа	700×2100	0
Д-4	дверь скрытого монтажа	700×2100	0
Д-5	дверь скрытого монтажа	550×2100	0

Ведомость отделки (на листе)

Марка	Поверхность	Материал, изделие	Цвет, код	Кол.
О5	стены	окраска, Tikkurila, шелковисто-матовая, подготовка Q3	NCS S 1502-Y50R	8,1 м²
О6	плинтус	плинтус МДФ, Orac Decor Contour (Luxxus), h 69 мм, SX165, шелковисто-матовая	NCS S 0300-N	2,7 м
О7	потолок	окраска, Tikkurila, глубокоматовая	NCS S 0300-N	5,5 м²

Схема развёрток (М 1:50)

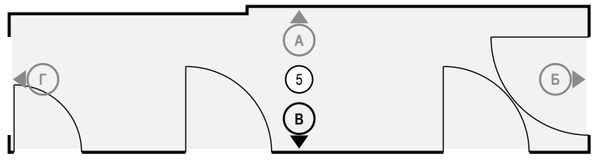


Примечания

1. Размеры — в мм от чистовых поверхностей стен; условные обозначения и общие указания — лист 14.
2. Двери скрытого монтажа — полотно в плоскости стены, отделка стены по полотну, плинтус прерывается у короба (узел — на листе узлов).


	Лист	№ док.	Подпись	Дата	Проект: Квартира 65 м²	М 1:20		
Дизайнер	Кырлан А.С.			14.11.26	Развёртка стены В. Коридор (пом. 5)	Стадия	Лист	Листов
Проверил						П	70	105
Н. контр.								
Утв.								

выпуск 14.11.2026 № 3aed0ef730 · стр. 70 из 105

Стена А (М 1:20)

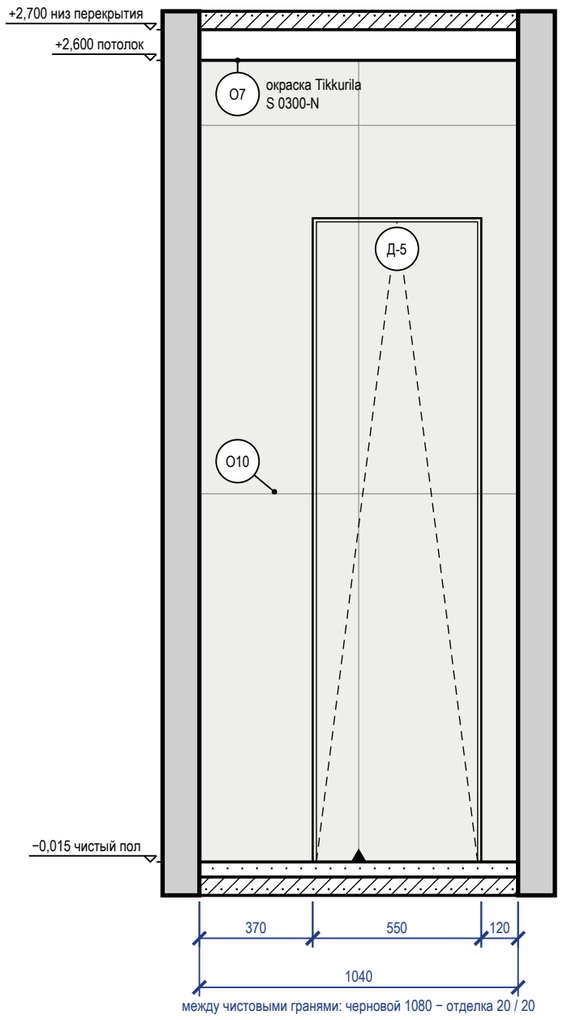

Стена Б (М 1:20)

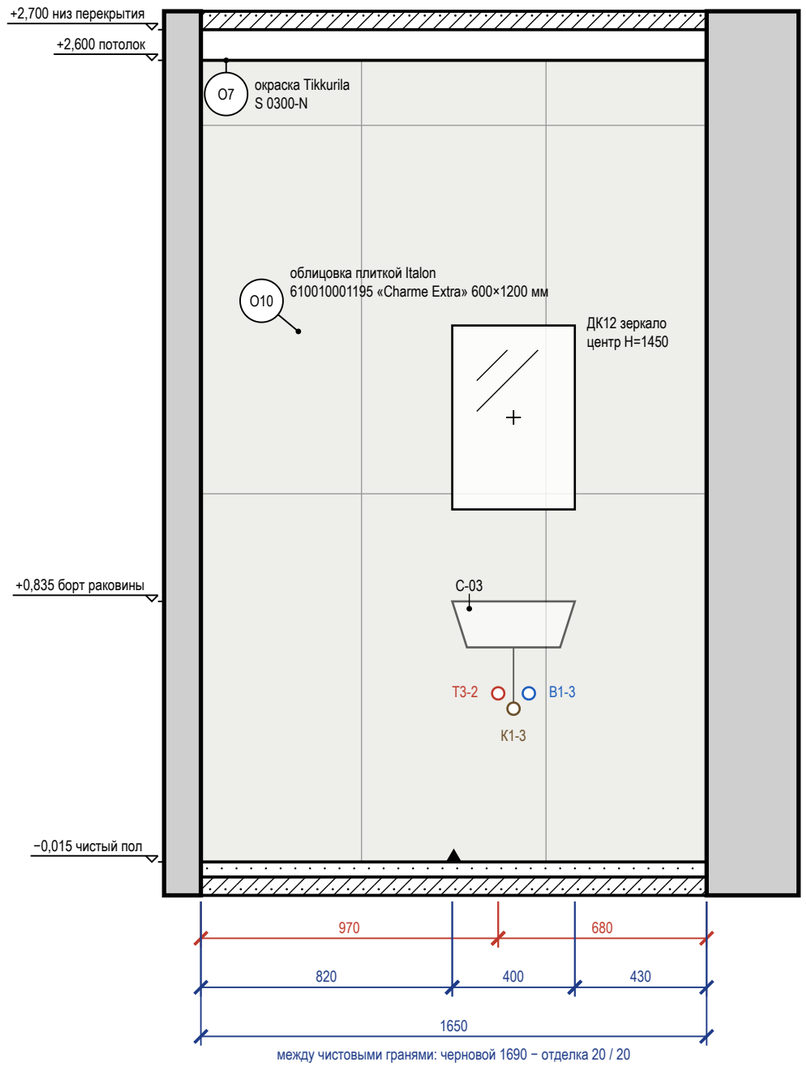

Ведомость точек и выводов

Стена	Марка	Что это	Гр.	H, мм	От угла, мм	Примечание
Б	Т3-2	горячая вода — умывальник		550	970	межос. 100
Б	К1-3	канализация — умывальник		500	1020	Ø50
Б	В1-3	холодная вода — умывальник		550	1070	межос. 100


Стена Б — визуализация, лист 9



Ведомость отделки (на листе)

Марка	Поверхность	Материал, изделие	Цвет, код	Кол.
О7	потолок	окраска, Tikkurila, глубокоматовая	NCS S 0300-N	1,8 м²
О10	стены	облицовка плиткой, Italon Charme Extra, 600×1200 мм, 610010001195	Italon 610010001195 «Charme Extra»	5,9 м²

Схема развёрток (М 1:50)

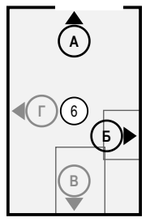

Ведомость изделий и проёмов (на листе)

Стена	Марка	Изделие, проём	На виде Ш×В, мм	Низ, мм
А	Д-5	дверь скрытого монтажа	550×2100	0
Б	С-03	умывальник	400×150	700
Б	ДК12	зеркало	400×600	1150


Примечания

1. Размеры — в мм от чистовых поверхностей стен; условные обозначения и общие указания — лист 14.
2. Облицовка — по сетке швов, раскладка от оси стены (треугольник у пола); подрезки — по листу раскладки плитки.
3. Гидроизоляция в 2 слоя, заход на стены 200 мм — до облицовки, с актом скрытых работ и тестом проливом (узел — на листе узлов).
4. Картины и зеркала крепить к основанию по паспорту изделия (закладные и анкеры — в перечне скрытых работ); крест — ось центра предмета.
5. Двери скрытого монтажа — полотно в плоскости стены, отделка стены по полотну, плинтус прерывается у короба (узел — на листе узлов).


	Лист	№ док.	Подпись	Дата	Проект: Квартира 65 м²	М 1:20		
Дизайнер	Кырлан А.С.			14.11.26	Развёртки стен А, Б. Санузел (пом. 6)	Стадия	Лист	Листов
Проверил						П	71	105
Н. контр.								
Утв.								

выпуск 14.11.2026 № 3aed0ef730 · стр. 71 из 105

Стена В (М 1:20)

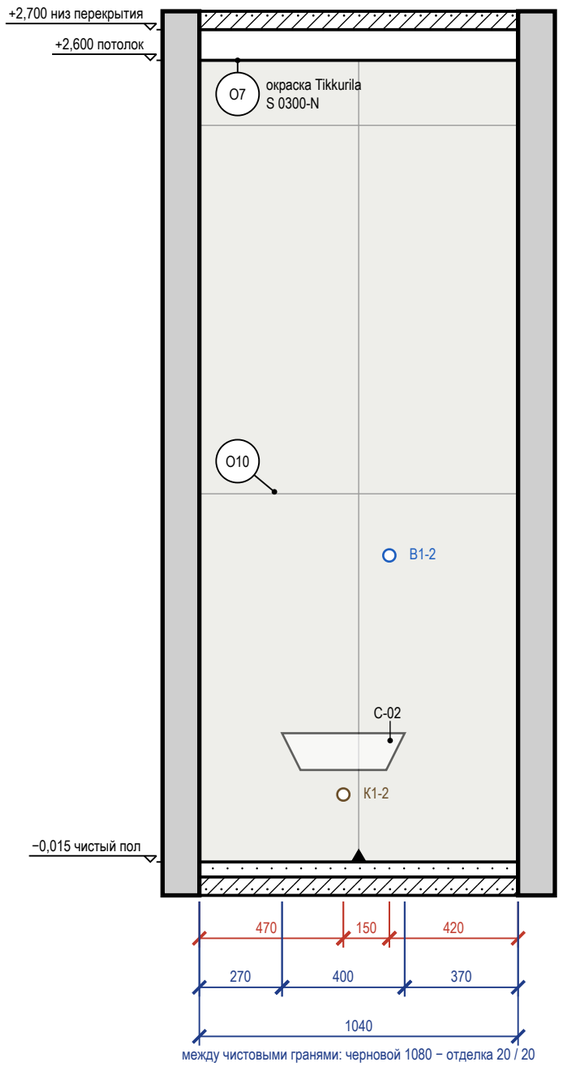

Стена Г (М 1:20)

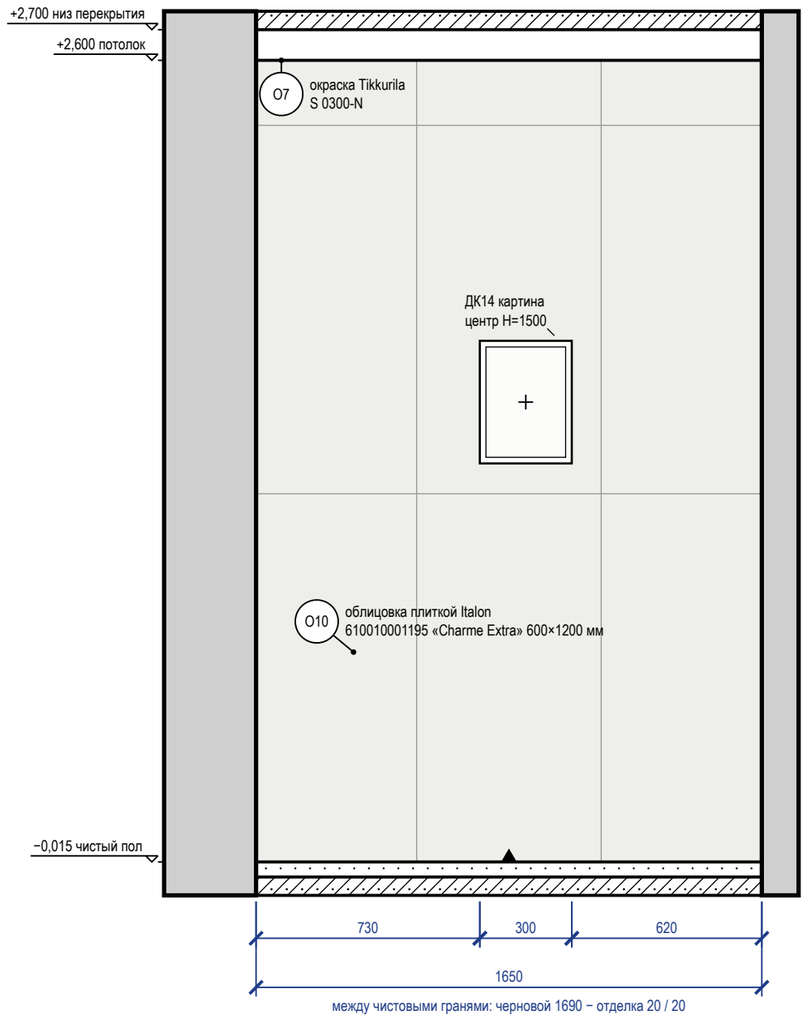


Ведомость точек и выводов

Стена	Марка	Что это	Гр.	Н, мм	От угла, мм	Примечание
В	К1-2	канализация — унитаз подвесной		220	470	Ø110
В	В1-2	холодная вода — унитаз подвесной		1000	620	в раме инсталляции

Ведомость отделки (на листе)

Марка	Поверхность	Материал, изделие	Цвет, код	Кол.
О7	потолок	окраска, Tikkurila, глубокоматовая	NCS S 0300-N	1,8 м²
О10	стены	облицовка плиткой, Italon Charme Extra, 600×1200 мм, 610010001195	Italon 610010001195 «Charme Extra»	7 м²

Схема развёрток (М 1:50)

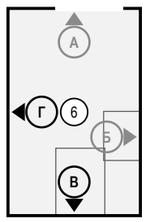

Ведомость изделий и проёмов (на листе)


Стена	Марка	Изделие, проём	На виде Ш×В, мм	Низ, мм
В	С-02	унитаз подвесной	400×120	300
Г	ДК14	картина	300×400	1300

Примечания

1. Размеры — в мм от чистовых поверхностей стен; условные обозначения и общие указания — лист 14.
2. Схема мебели, приборов и декора не является технической документацией для производства мебели; габариты — по паспортам изделий.
3. Облицовка — по сетке швов, раскладка от оси стены (треугольник у пола); подрезки — по листу раскладки плитки.
4. Гидроизоляция в 2 слоя, заход на стены 200 мм — до облицовки, с актом скрытых работ и тестом проливом (узел — на листе узлов).
5. Картины и зеркала крепить к основанию по паспорту изделия (закладные и анкеры — в перечне скрытых работ); крест — ось центра предмета.


	Лист	№ док.	Подпись	Дата	Проект: Квартира 65 м²	М 1:20
Дизайнер	Кырлан А.С.			14.11.26	Развёртки стен В, Г. Санузел (пом. 6)	Стадия: П; Лист: 72; Листов: 105
Проверил						
Н. контр.						
Утв.						

Стена А (М 1:20)

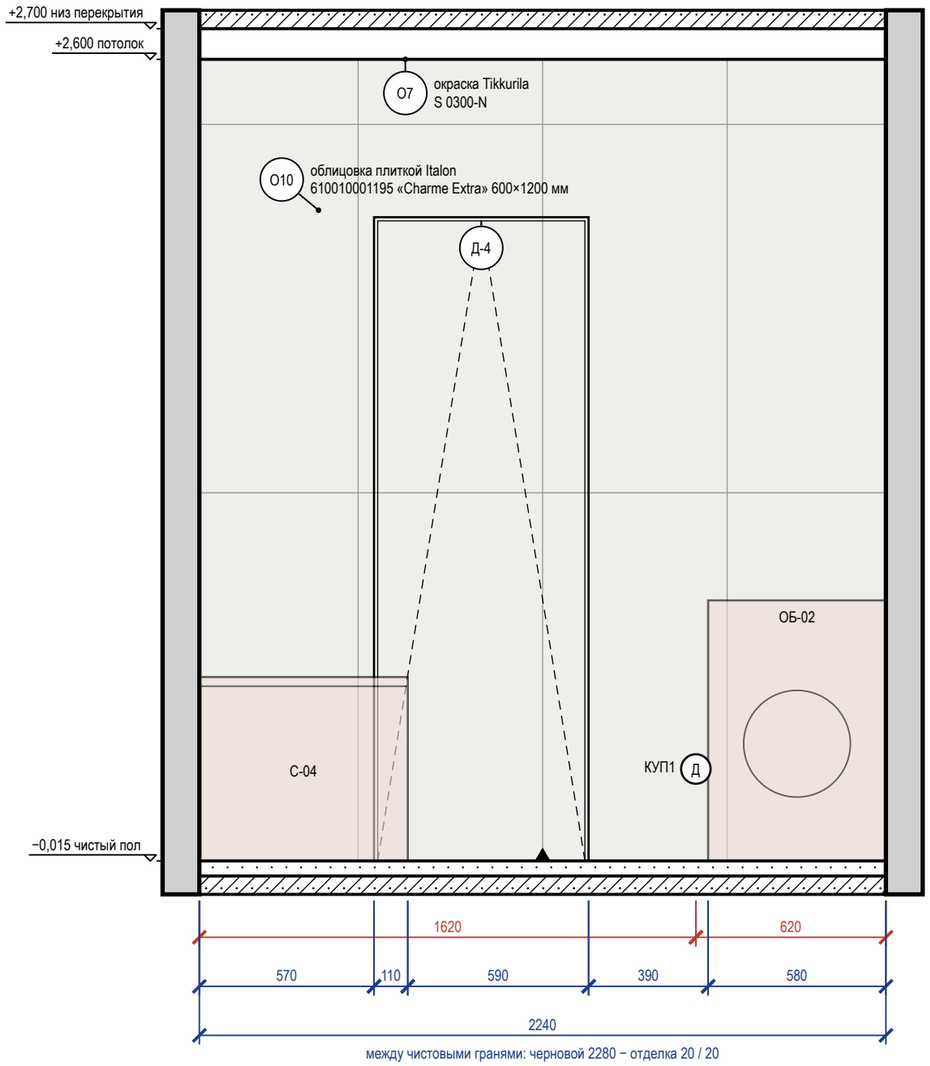


между чистовыми гранями: черновой 2280 − отделка 20 / 20

Стена Б (М 1:20)

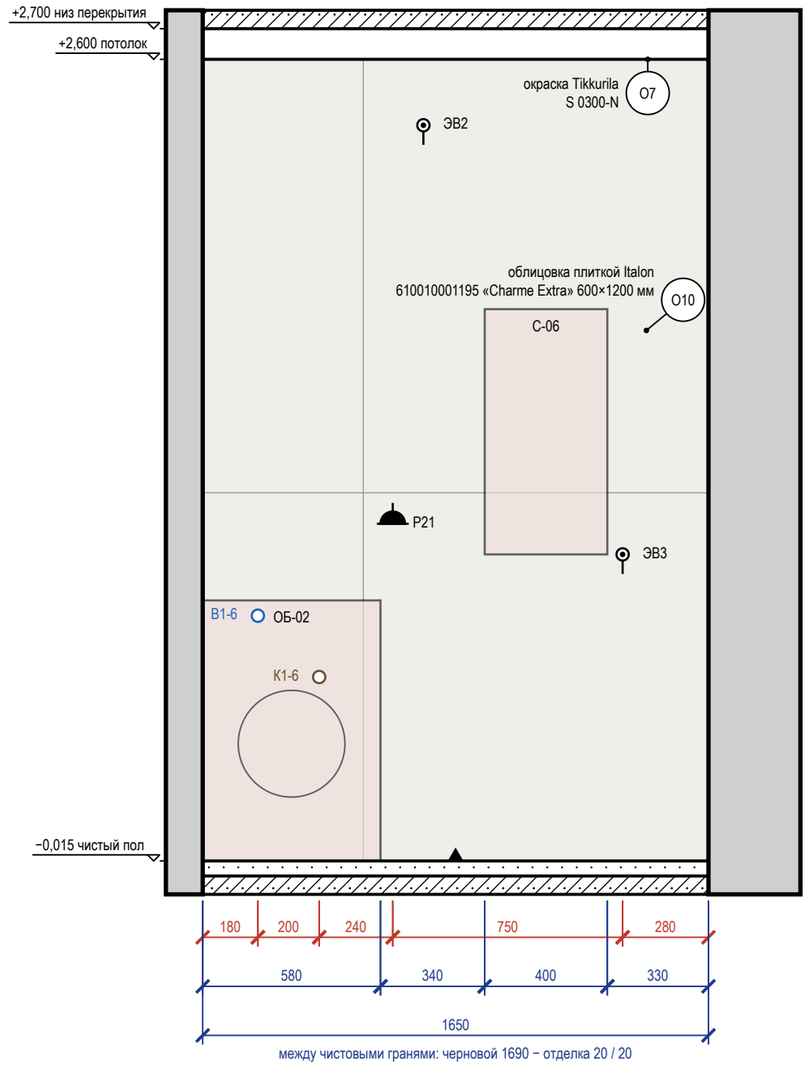

между чистовыми гранями: черновой 1690 − отделка 20 / 20

Схема развёрток (М 1:50)

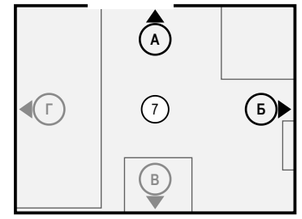

Ведомость точек и выводов

Стена	Марка	Что это	Гр.	Н, мм	От угла, мм	Примечание
А	КУП1	КУП (уравнивание потенциалов)		300	1620	
Б	В1-6	холодная вода — стиральная машина		800	180	кран машины
Б	К1-6	канализация — стиральная машина		600	380	Ø50
Б	Р21	розетка: стиральная машина	5	1100	620	IP44
Б	ЭВ2	вывод кабеля: вентилятор (клавиша L4, таймер выбега)	1	2400	720	
Б	ЭВ3	вывод кабеля: полотенцесушитель	5	1000	1370	

Ведомость отделки (на листе)

Марка	Поверхность	Материал, изделие	Цвет, код	Кол.
О7	потолок	окраска, Tikkurila, глубокоматовая	NCS S 0300-N	3,9 м²
О10	стены	облицовка плиткой, Italon Charme Extra, 600×1200 мм, 610010001195	Italon 610010001195 «Charme Extra»	8,7 м²

Ведомость изделий и проёмов (на листе)

Стена	Марка	Изделие, проём	На виде Ш×В, мм	Низ, мм
А	С-04	ванна	680×600	0
А	Д-4	дверь скрытого монтажа	700×2100	0
А	ОБ-02	стиральная машина	580×850	0
Б	ОБ-02	стиральная машина	580×850	0
Б	С-06	полотенцесушитель	400×800	1000

Примечания

1. Размеры — в мм от чистовых поверхностей стен; условные обозначения и общие указания — лист 14.
2. Схема мебели, приборов и декора не является технической документацией для производства мебели; габариты — по паспортам изделий.
3. Облицовка — по сетке швов, раскладка от оси стены (треугольник у пола); подрезки — по листу раскладки плитки.
4. Гидроизоляция в 2 слоя, заход на стены 200 мм; над ванной — до 2000 и 300 мм за борт — до облицовки, с актом скрытых работ и тестом проливом (узел — на листе узлов).
5. Двери скрытого монтажа — полотно в плоскости стены, отделка стены по полотну, плинтус прерывается у короба (узел — на листе узлов).

	Лист	№ док.	Подпись	Дата
Дизайнер	Кырлан А.С.			14.11.26
Проверил				
Н. контр.				
Утв.				


Проект: Квартира 65 м² — **М 1:20**

Развёртки стен А, Б. Ванная (пом. 7)

Стадия	Лист	Листов
П	73	105

выпуск 14.11.2026 № 3aed0ef730 · стр. 73 из 105

Стена В (М 1:20)

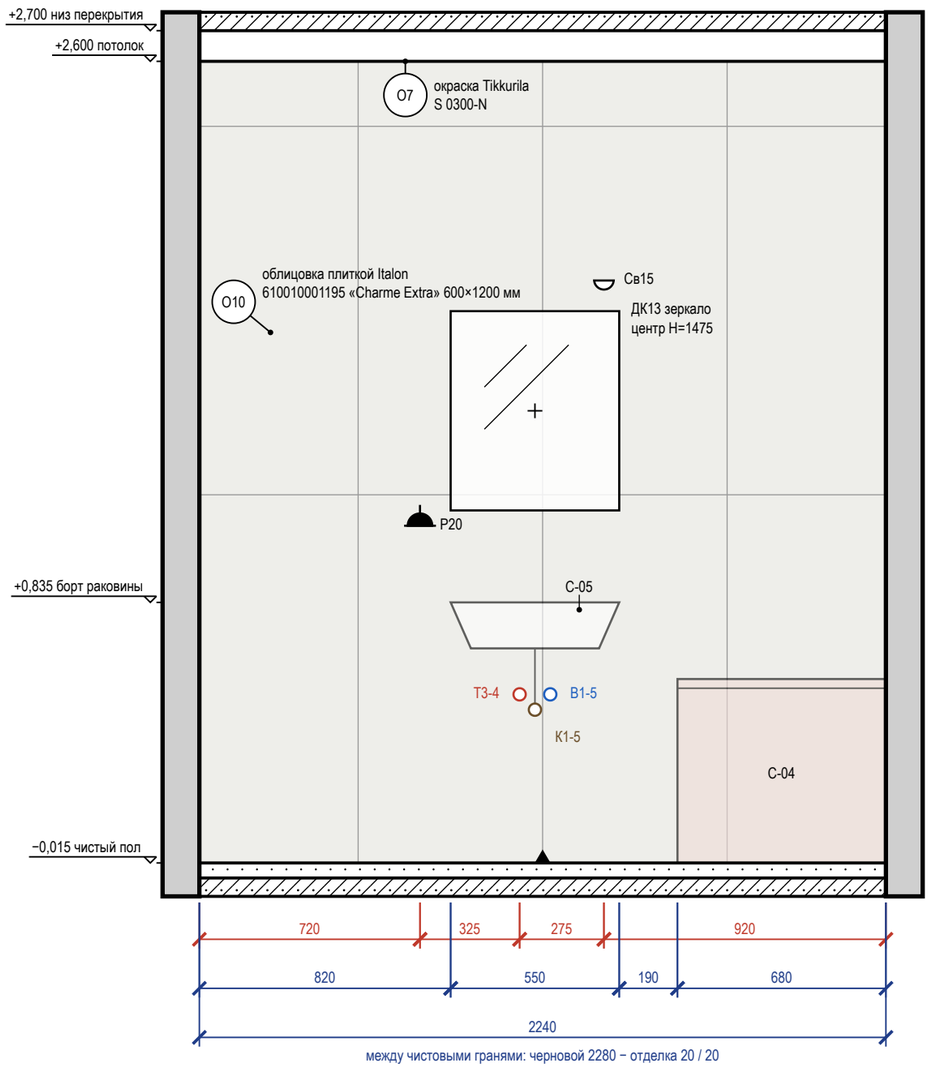

Ведомость точек и выводов

Марка	Что это	Гр.	H, мм	От угла, мм	Примечание
Р20	розетка: фен	5	1100	720	IP44
Т3-4	горячая вода — умывальник		550	1045	межос. 100
К1-5	канализация — умывальник		500	1095	Ø50
В1-5	холодная вода — умывальник		550	1145	межос. 100
Св15	светильник настенный	1	1900	1320	


Стена В — визуализация, лист 10



Ведомость отделки (на листе)

Марка	Поверхность	Материал, изделие	Цвет, код	Кол.
О7	потолок	окраска, Tikkurila, глубокоматовая	NCS S 0300-N	3,9 м²
О10	стены	облицовка плиткой, Italon Charme Extra, 600×1200 мм, 610010001195	Italon 610010001195 «Charme Extra»	5,9 м²

Схема развёрток (М 1:50)

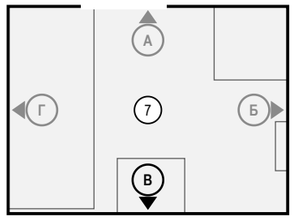

Ведомость изделий и проёмов (на листе)


Марка	Изделие, проём	На виде Ш×В, мм	Низ, мм
С-05	умывальник	550×150	700
ДК13	зеркало	550×650	1150
С-04	ванна	680×600	0

Примечания

1. Размеры — в мм от чистовых поверхностей стен; условные обозначения и общие указания — лист 14.
2. Облицовка — по сетке швов, раскладка от оси стены (треугольник у пола); подрезки — по листу раскладки плитки.
3. Гидроизоляция в 2 слоя, заход на стены 200 мм; над ванной — до 2000 и 300 мм за борт — до облицовки, с актом скрытых работ и тестом проливом (узел — на листе узлов).
4. Картины и зеркала крепить к основанию по паспорту изделия (закладные и анкеры — в перечне скрытых работ); крест — ось центра предмета.


	Лист	№ док.	Подпись	Дата	Проект: Квартира 65 м²			М 1:20
Дизайнер	Кырлан А.С.			14.11.26	Развёртка стены В. Ванная (пом. 7)	Стадия	Лист	Листов
Проверил						П	74	105
Н. контр.								
Утв.								

Стена Г (М 1:20)

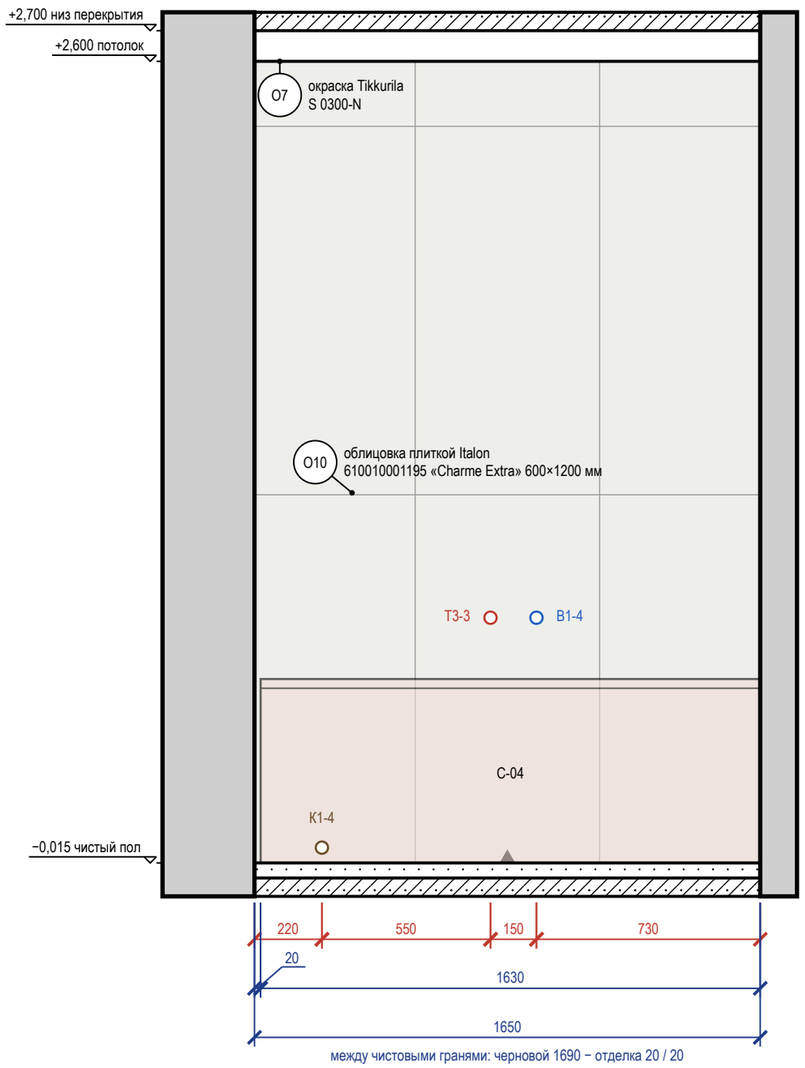

4 Гидроизоляция санузла: заход на стены 200 мм, примыкание ванны (М 1:10)

Узел 4 — лист С13

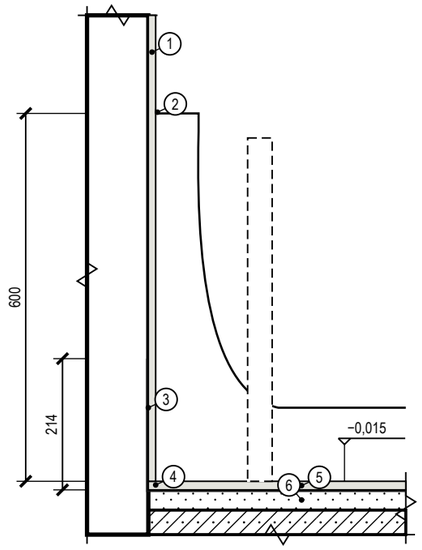

Поз.	Состав слоя, изделие
1	облицовка — плитка на клею С2 TE S1, затирка CG2WA
2	примыкание ванны: лента бордюрная + силиконовый санитарный герметик; облицовка опирается на борт
3	гидроизоляция обмазочная в 2 слоя, заход на стены 200 мм (в зоне душа — выше), до облицовки; акт скрытых работ, тест проливом
4	лента гидроизоляционная в углах и у трапов
5	керамогранит на клею С2 TE S1
6	ЦПС М200 33 мм

Ведомость точек и выводов

Марка	Что это	Гр.	Н, мм	От угла, мм	Примечание
К1-4	канализация — ванна		50	220	Ø50
Т3-3	горячая вода — ванна		800	770	межос. 150
В1-4	холодная вода — ванна		800	920	межос. 150


Ведомость изделий и проёмов (на листе)

Марка	Изделие, проём	На виде Ш×В, мм	Низ, мм
С-04	ванна	1630×600	0

Ведомость отделки (на листе)

Марка	Поверхность	Материал, изделие	Цвет, код	Кол.
О7	потолок	окраска, Tikkurila, глубокоматовая	NCS S 0300-N	3,9 м²
О10	стены	облицовка плиткой, Italon Charme Extra, 600×1200 мм, 610010001195	Italon 610010001195 «Charme Extra»	4,3 м²

Схема развёрток (М 1:50)

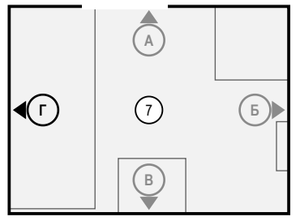

Примечания

1. Размеры — в мм от чистовых поверхностей стен; условные обозначения и общие указания — лист 14.
2. Облицовка — по сетке швов, раскладка от оси стены (треугольник у пола); подрезки — по листу раскладки плитки.
3. Гидроизоляция в 2 слоя, заход на стены 200 мм; над ванной — до 2000 и 300 мм за борт — до облицовки, с актом скрытых работ и тестом проливом (узел — на листе узлов).

	Лист	№ док.	Подпись	Дата
Дизайнер	Кырлан А.С.			14.11.26
Проверил				
Н. контр.				
Утв.				


Проект: Квартира 65 м² — М 1:20

Развёртка стены Г. Ванная (пом. 7)

Стадия	Лист	Листов
П	75	105


выпуск 14.11.2026 № 3aed0ef730 · стр. 75 из 105

Стена А (М 1:20)

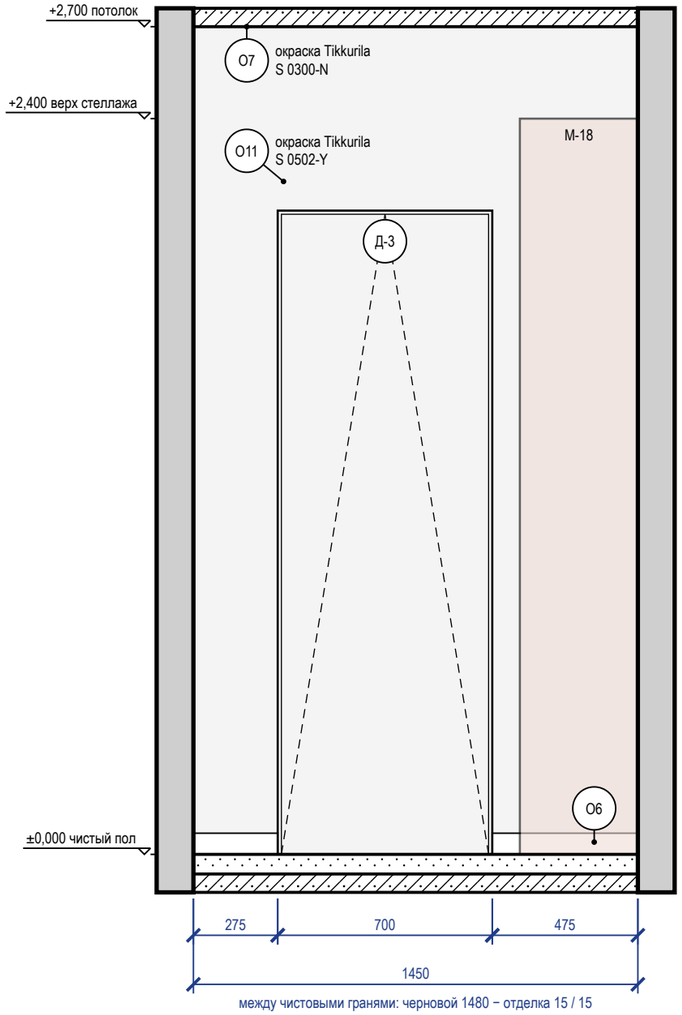


между чистовыми гранями: черновой 1480 − отделка 15 / 15

Стена Б (М 1:20)

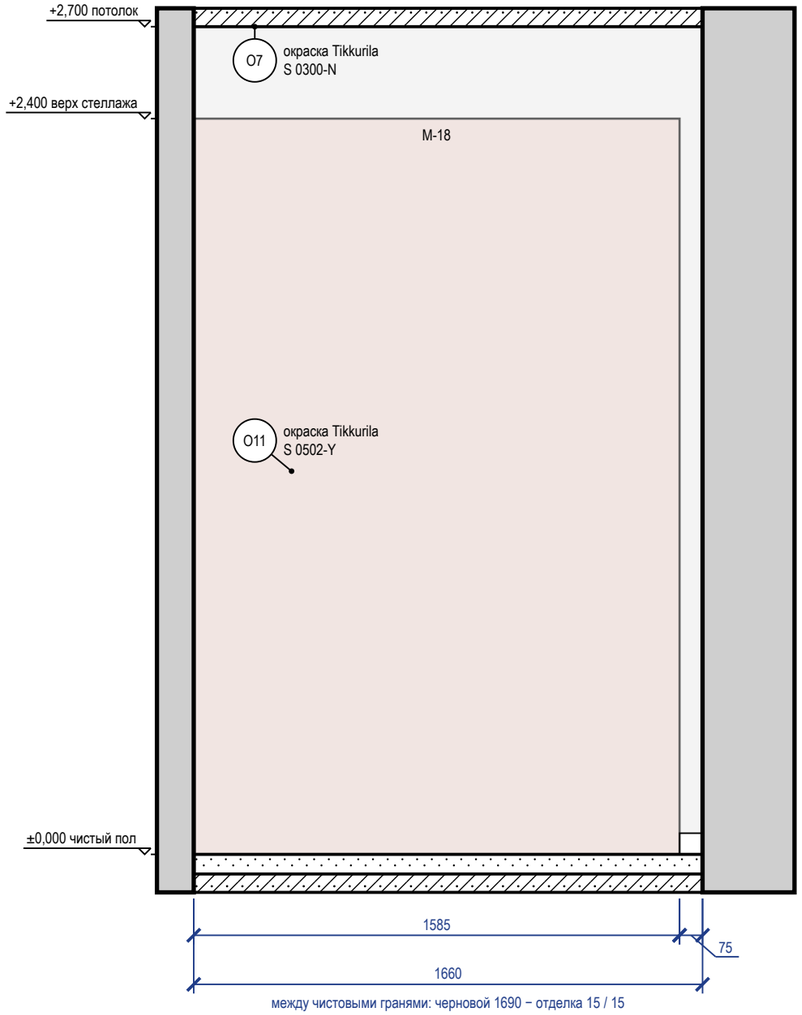

между чистовыми гранями: черновой 1690 − отделка 15 / 15

Стена В (М 1:20)

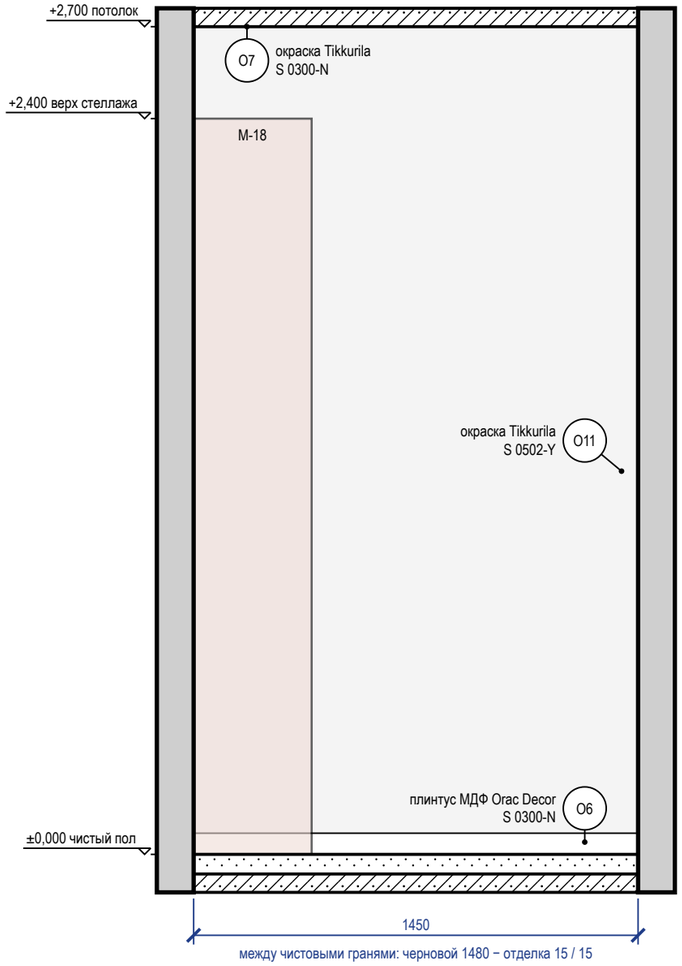

между чистовыми гранями: черновой 1480 − отделка 15 / 15


Стена В — визуализация, лист 11



Ведомость отделки (на листе)

Марка	Поверхность	Материал, изделие	Цвет, код	Кол.
О6	плинтус	плинтус МДФ, Orac Decor Contour (Luxxus), h 69 мм, SX165, шелковисто-матовая	NCS S 0300-N	2,3 м
О7	потолок	окраска, Tikkurila, глубокоматовая	NCS S 0300-N	2,5 м²
О11	стены	окраска, Tikkurila, матовая, подготовка Q3	NCS S 0502-Y	10,8 м²

Схема развёрток (М 1:50)

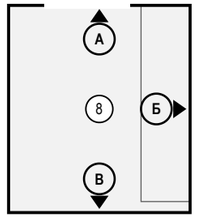


Примечания

1. Размеры — в мм от чистовых поверхностей стен; условные обозначения и общие указания — лист 14.
2. Двери скрытого монтажа — полотно в плоскости стены, отделка стены по полотну, плинтус прерывается у короба (узел — на листе узлов).

	Лист	№ док.	Подпись	Дата	Проект: Квартира 65 м²			М 1:20
Дизайнер	Кырлан А.С.			14.11.26	Развёртки стен. Кладовая (пом. 8)	Стадия	Лист	Листов
Проверил						П	76	105
Н. контр.								
Утв.								

выпуск 14.11.2026 № 3aed0ef730 · стр. 76 из 105

Стена А (М 1:20)

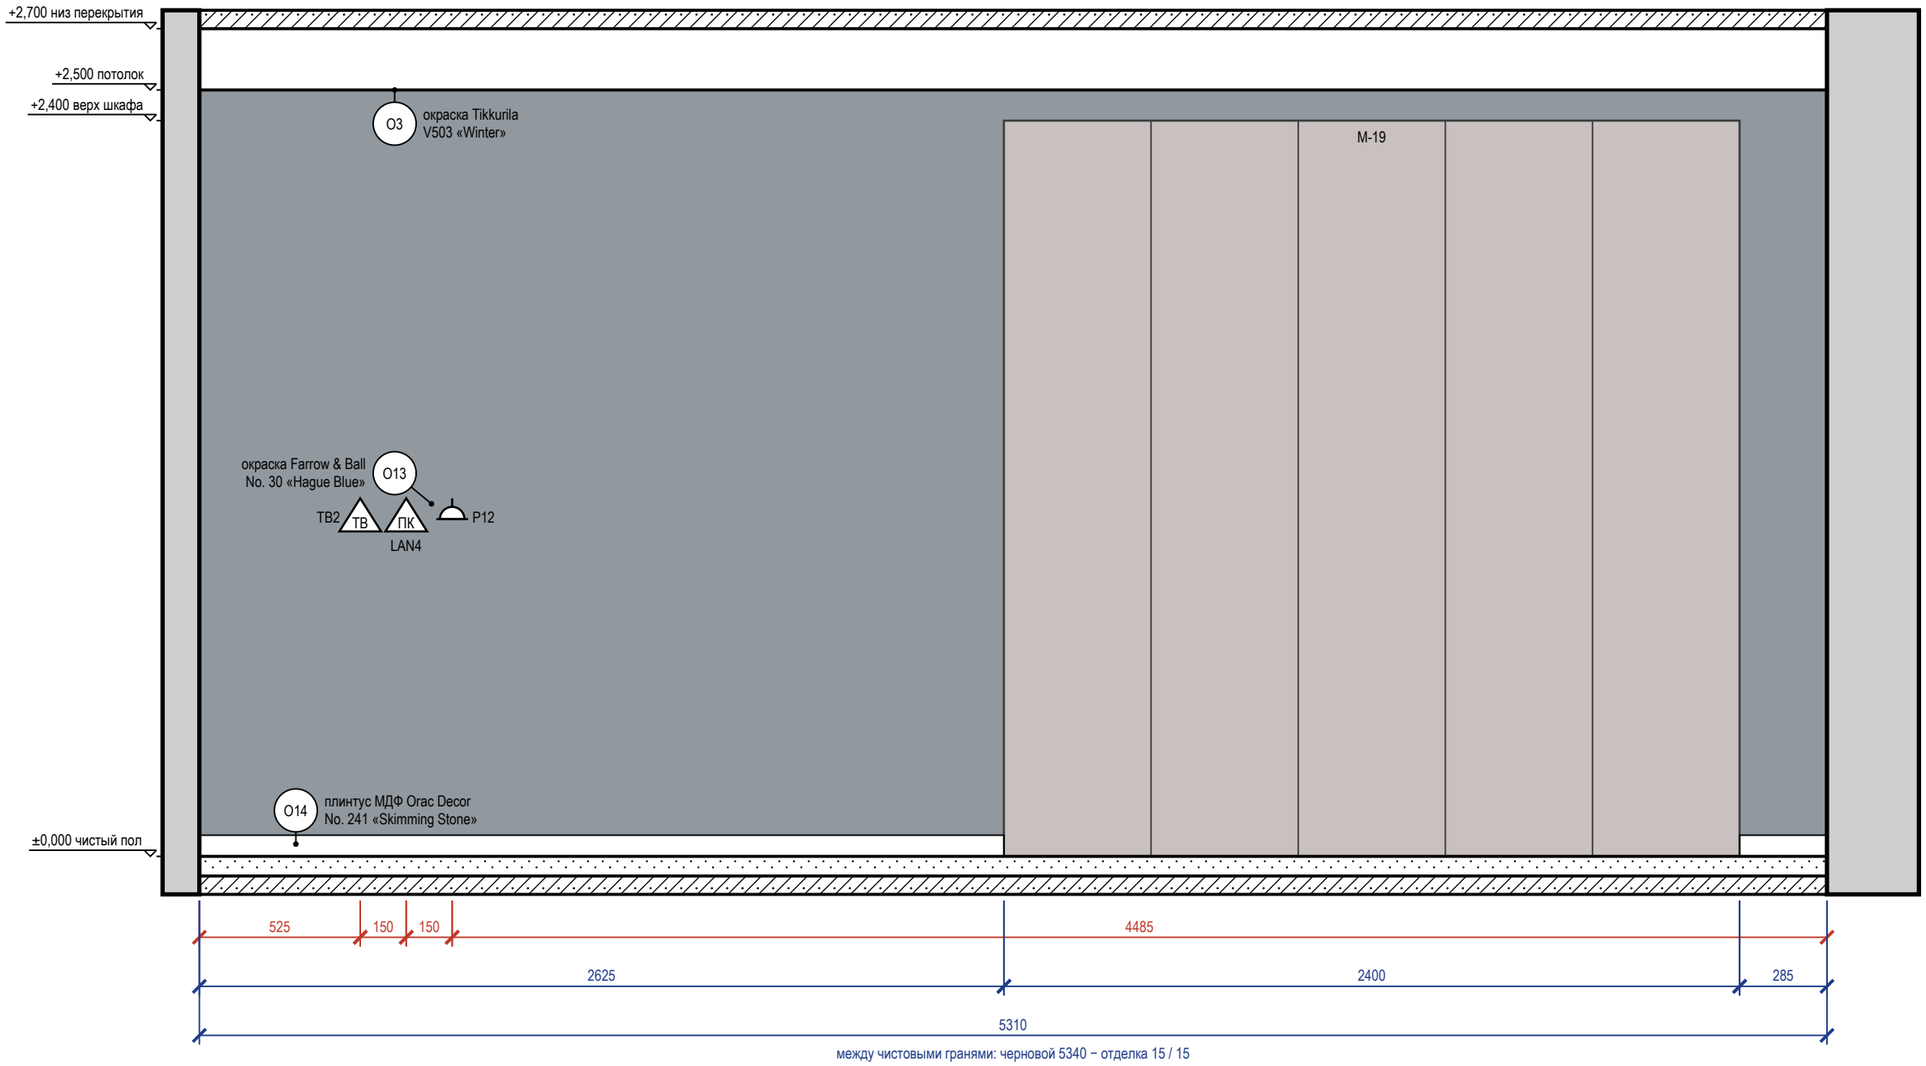


Ведомость точек и выводов

Марка	Что это	Гр.	Н, мм	От угла, мм	Примечание
ТВ2	розетка ТВ: ТВ на стене А, кронштейн (мебели под ТВ нет)		1100	525	
LAN4	розетка RJ45: Smart TV		1100	675	
Р12	розетка: ТВ (в одной зоне с ТВ2, LAN4 на стене А)	5	1100	825	

Ведомость отделки (на листе)

Марка	Поверхность	Материал, изделие	Цвет, код	Кол.
О3	потолок	окраска, Tikkurila Anti-Reflex 2, глубокоматовая, подготовка Q3	Tikkurila V503 «Winter»	16 м²
О13	акцентная стена	окраска, Farrow & Ball Modern Emulsion, матовая, подготовка Q3	Farrow & Ball No. 30 «Hague Blue»	13,3 м²
О14	плинтус	плинтус МДФ, Orac Decor Contour (Luxxus), h 69 мм, SX165	Farrow & Ball No. 241 «Skimming Stone»	2,9 м

Схема развёрток (М 1:100)

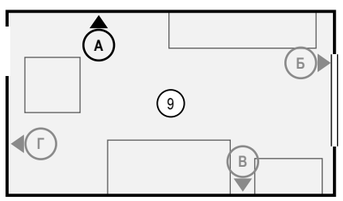

Примечания

1. Размеры — в мм от чистовых поверхностей стен; условные обозначения и общие указания — лист 14.
2. Потолок — у каждой стены свой, по плану потолков (ПТ3); ступени — зоной, кромка короба перед нишей — тонкой линией; в поле потолка: ПТ1 +2,600.

	Лист	№ док.	Подпись	Дата
Дизайнер	Кырлан А.С.			14.11.26
Проверил				
Н. контр.				
Утв.				


Проект: Квартира 65 м² — **М 1:20**

Развёртка стены А. Детская (пом. 9)

Стадия	Лист	Листов
П	77	105

выпуск 14.11.2026 № 3aed0ef730 · стр. 77 из 105

Стена Б (М 1:20)

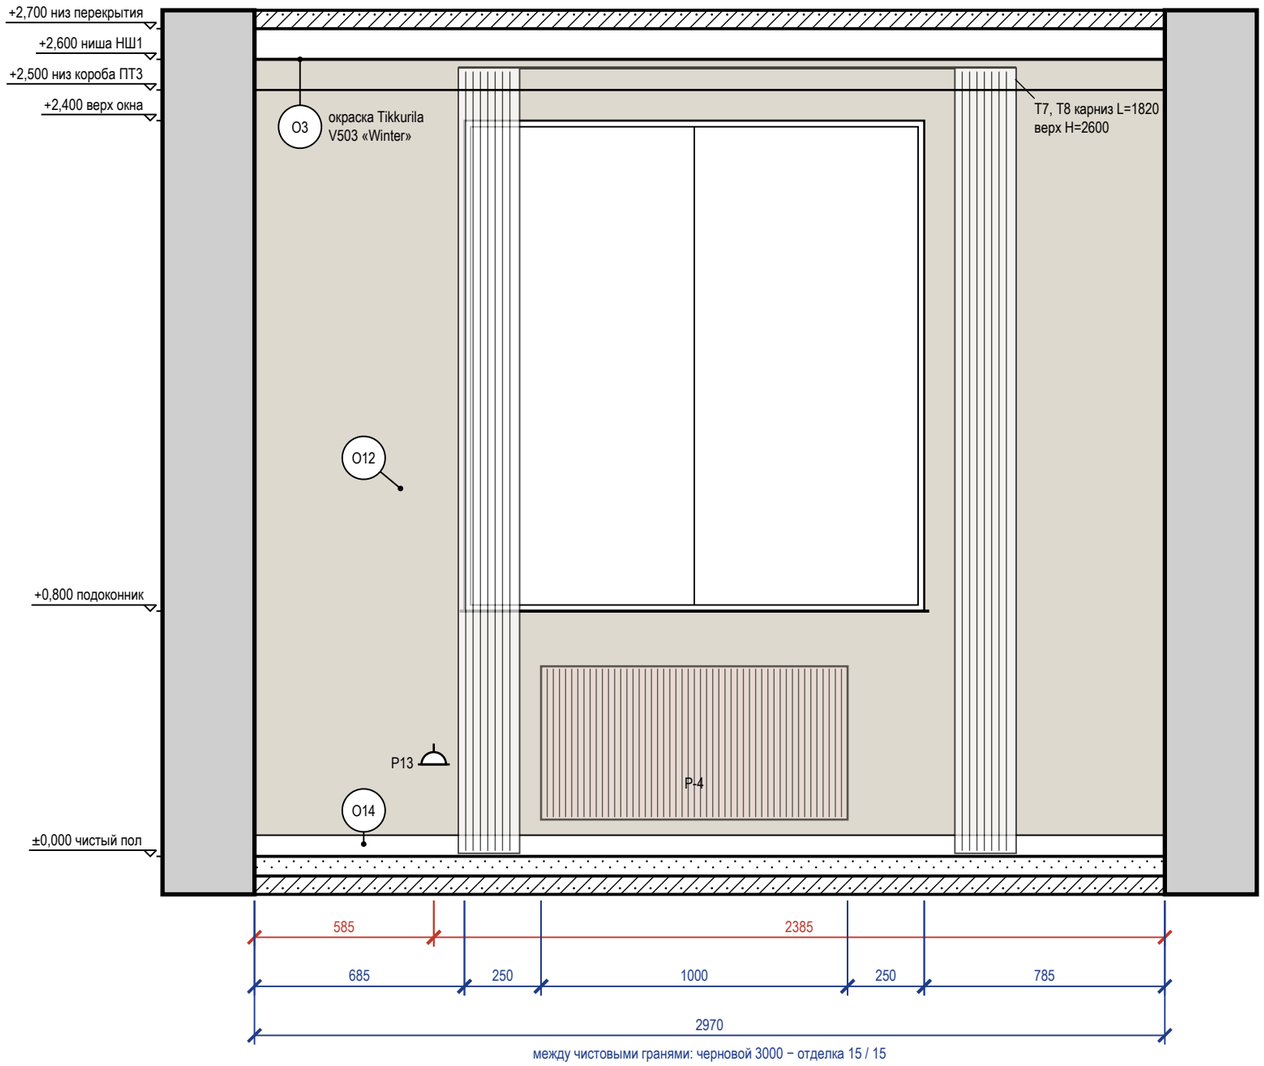

Ведомость точек и выводов

Марка	Что это	Гр.	Н, мм	От угла, мм	Примечание
Р13	розетка: уборка	5	300	585	


Ведомость изделий и проёмов (на листе)

Марка	Изделие, проём	На виде Ш×В, мм	Низ, мм
Р-4	радиатор отопления	1000×500	120


Ведомость отделки (на листе)

Марка	Поверхность	Материал, изделие	Цвет, код	Кол.
О3	потолок	окраска, Tikkurila Anti-Reflex 2, глубокоматовая, подготовка Q3	Tikkurila V503 «Winter»	16 м²
О12	стены	окраска, Farrow & Ball Modern Emulsion, матовая, подготовка Q3	Farrow & Ball No. 241 «Skimming Stone»	5,3 м²
О14	плинтус	плинтус МДФ, Orac Decor Contour (Luxxus), h 69 мм, SX165	Farrow & Ball No. 241 «Skimming Stone»	3 м

Схема развёрток (М 1:50)

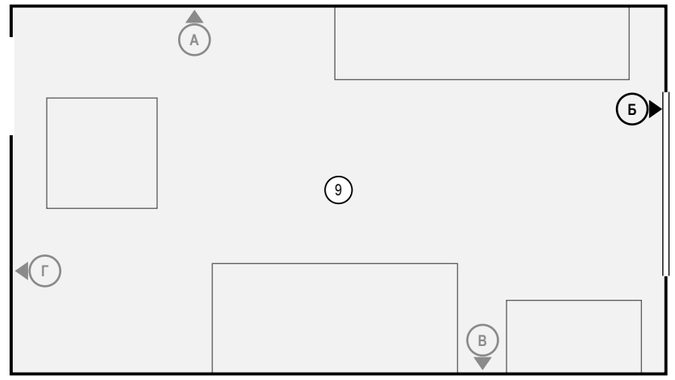

5 **Плинтус МДФ 69×16 мм у окрашенной стены по доске (ламинату) (М 1:10)**
Узел 5 — лист С13

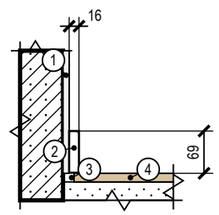

Поз.	Состав слоя, изделие
1	штукатурка, шпаклёвка Q3, окраска — по ведомости отделки
2	плинтус МДФ 69×16 под окраску в цвет стены; клей монтажный — к стене, не к полу
3	зазор покрытия у стены 8–10 мм закрывается плинтусом
4	инженерная доска на клею


Примечания

1. Размеры — в мм от чистовых поверхностей стен; условные обозначения и общие указания — лист 14.
2. Карнизы (шины) — по ведомости текстиля декоратора: длина L и верх H на развёртке — те же числа, что в ведомости; крепление — до окраски потолка.
3. Потолок — у каждой стены свой, по плану потолков (НШ1, ПТ3); ступени — зоной, кромка короба перед нишей — тонкой линией; в поле потолка: ПТ1 +2,600.

	Лист	№ док.	Подпись	Дата	Проект: Квартира 65 м²	М 1:20		
Дизайнер	Кырлан А.С.			14.11.26	Развёртка стены Б. Детская (пом. 9)	Стадия	Лист	Листов
Проверил						П	78	105
Н. контр.								
Утв.								

выпуск 14.11.2026 № 3aed0ef730 · стр. 78 из 105

Стена В (М 1:25)

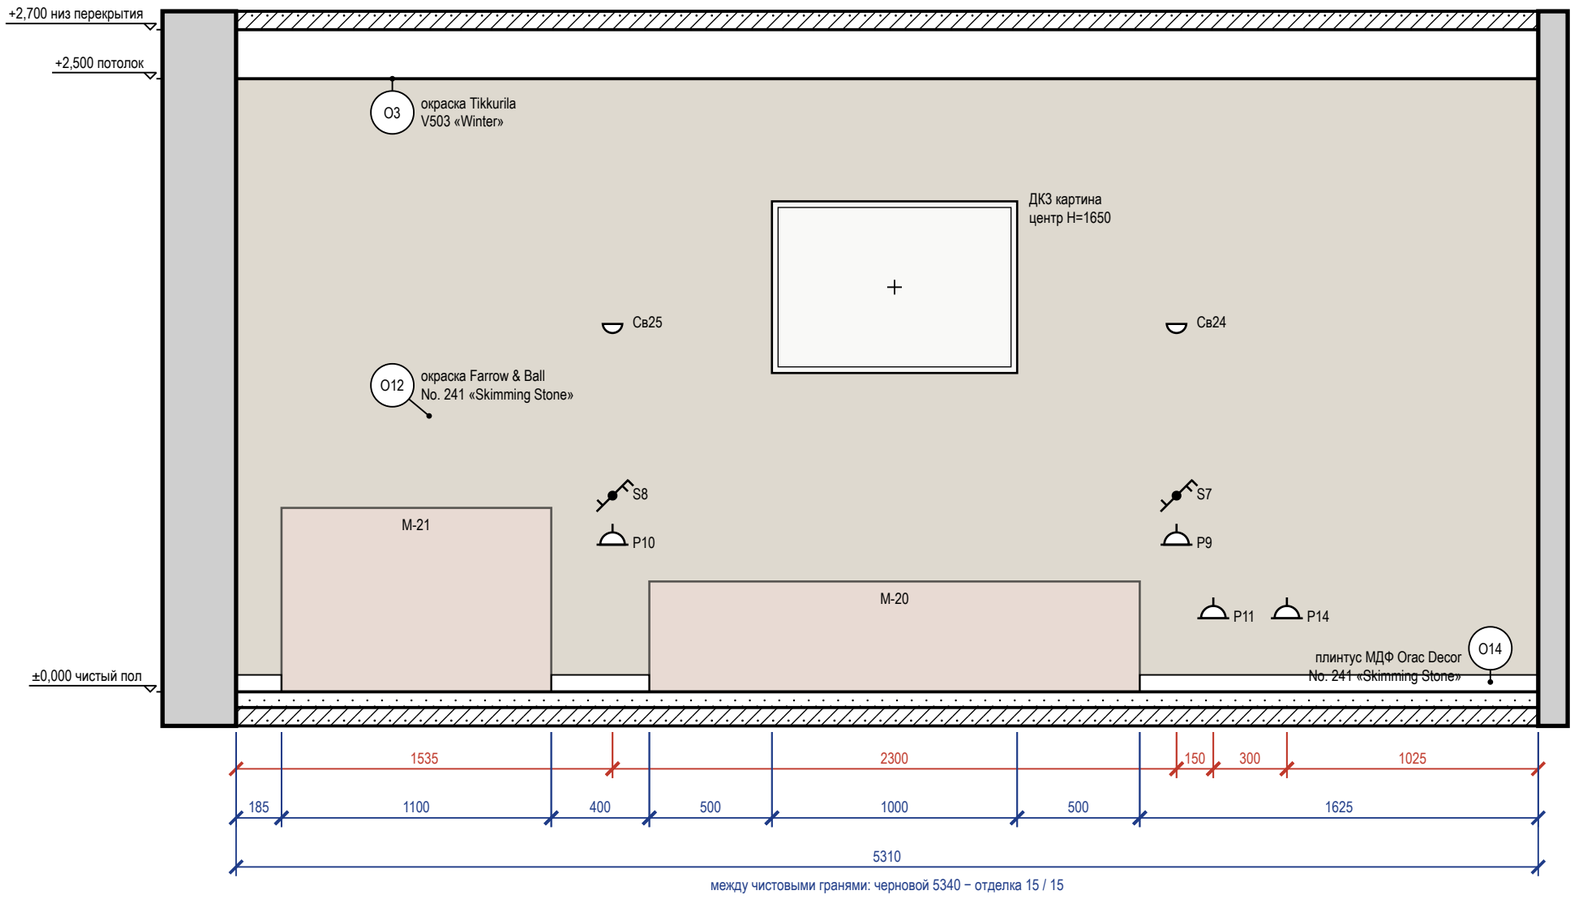

Ведомость точек и выводов

Марка	Что это	Гр.	H, мм	От угла, мм	Примечание
P10	розетка: у кровати	5	600	1535	
S8	выключатель	1	800	1535	
Св25	светильник настенный	1	1500	1535	
P9	розетка: у кровати	5	600	3835	
S7	выключатель	1	800	3835	
Св24	светильник настенный	1	1500	3835	
P11	розетка: торшер у кровати М-20 (изголовье)	5	300	3985	
P14	розетка: уборка у входа	5	300	4285	


Стена В — визуализация, лист 12



Ведомость отделки (на листе)

Марка	Поверхность	Материал, изделие	Цвет, код	Кол.
О3	потолок	окраска, Tikkurila Anti-Reflex 2, глубокоматовая, подготовка Q3	Tikkurila V503 «Winter»	16 м²
О12	стены	окраска, Farrow & Ball Modern Emulsion, матовая, подготовка Q3	Farrow & Ball No. 241 «Skimming Stone»	13,3 м²
О14	плинтус	плинтус МДФ, Orac Decor Contour (Luxxus), h 69 мм, SX165	Farrow & Ball No. 241 «Skimming Stone»	2,2 м

Схема развёрток (М 1:50)

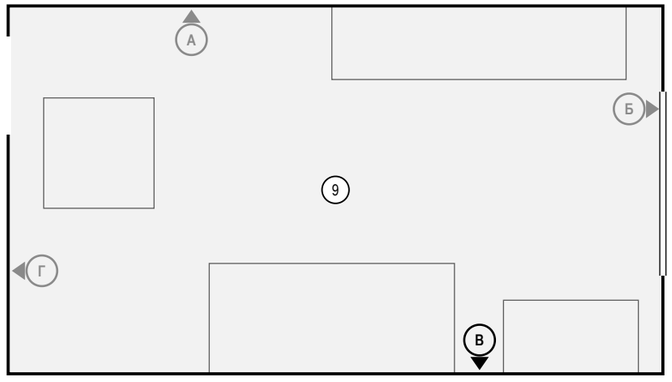

Ведомость изделий и проёмов (на листе)

Марка	Изделие, проём	На виде Ш×В, мм	Низ, мм
М-21	стол письменный	1100×750	0
М-20	кровать односпальная 900×2000	2000×450	0
ДК3	картина	1000×700	1300


Примечания

1. Размеры — в мм от чистовых поверхностей стен; условные обозначения и общие указания — лист 14.
2. Картины и зеркала крепить к основанию по паспорту изделия (закладные и анкеры — в перечне скрытых работ); крест — ось центра предмета.
3. Потолок — у каждой стены свой, по плану потолков (ПТ3); ступени — зоной, кромка короба перед нишей — тонкой линией; в поле потолка: ПТ1 +2,600.


	Лист	№ док.	Подпись	Дата	Проект: Квартира 65 м²	М 1:25		
Дизайнер	Кырлан А.С.			14.11.26	Развёртка стены В. Детская (пом. 9)	Стадия	Лист	Листов
Проверил						П	79	105
Н. контр.								
Утв.								

выпуск 14.11.2026 № 3aed0ef730 · стр. 79 из 105

Стена Г (М 1:20)

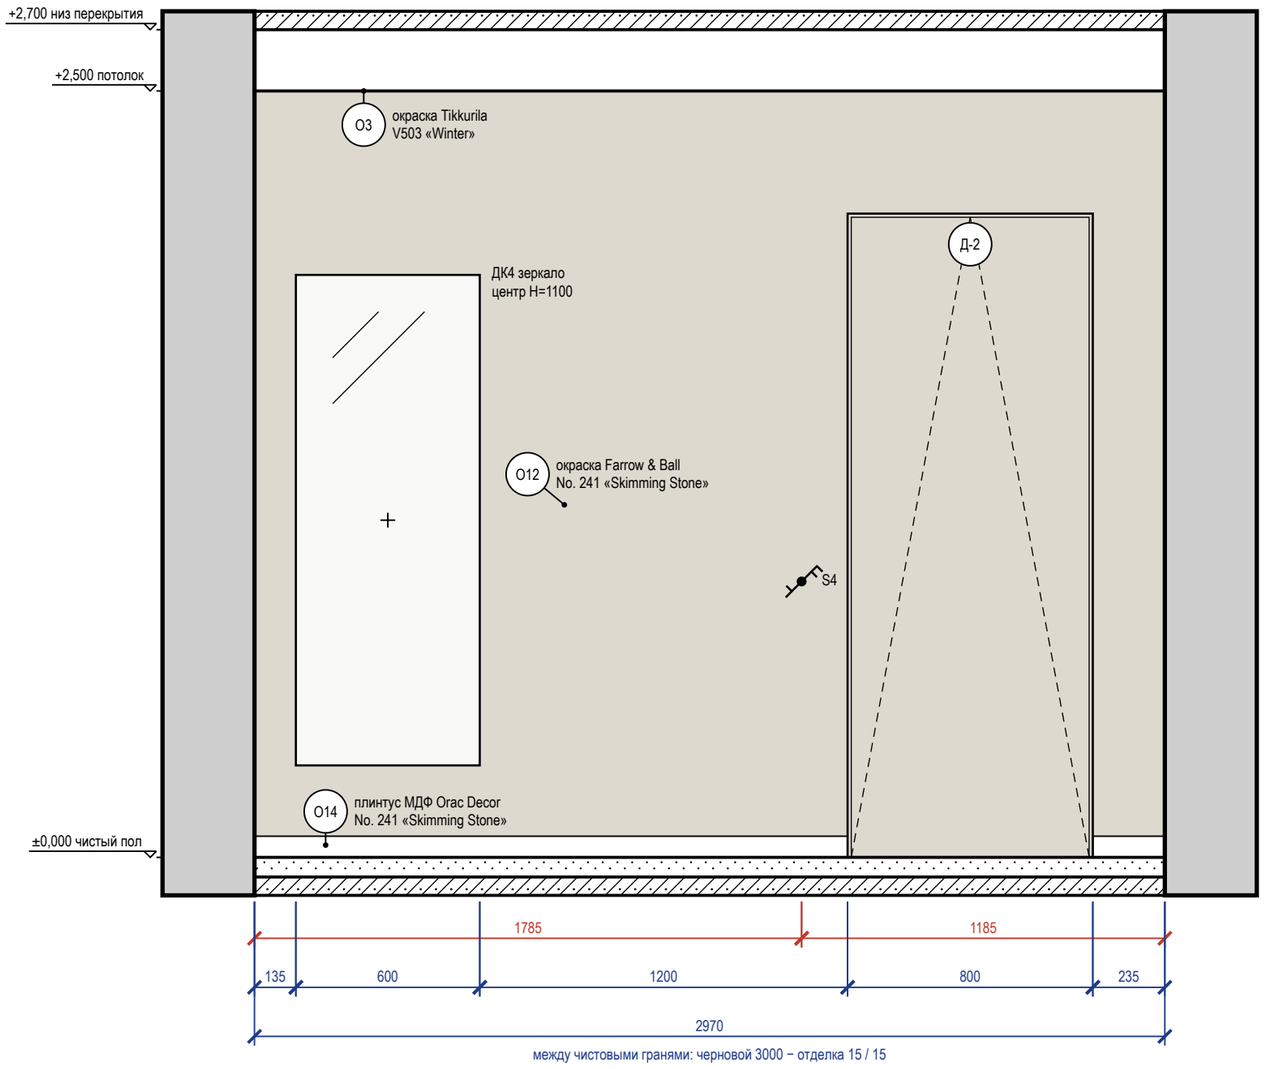

Стена Г — визуализация, лист 13

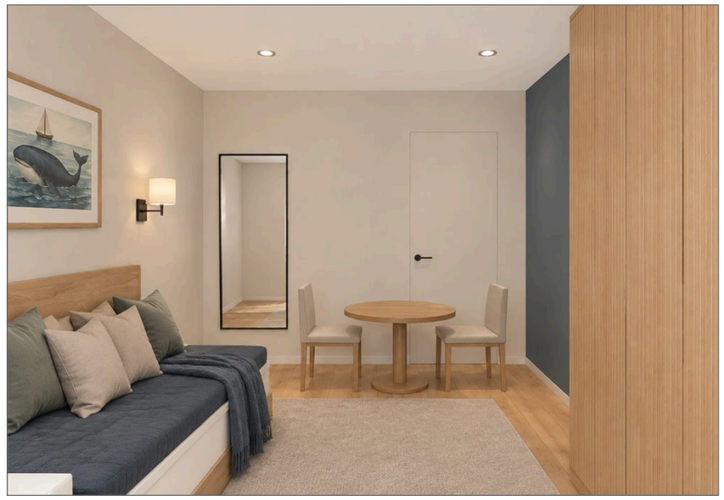

Ведомость отделки (на листе)

Марка	Поверхность	Материал, изделие	Цвет, код	Кол.
О3	потолок	окраска, Tikkurila Anti-Reflex 2, глубокоматовая, подготовка Q3	Tikkurila V503 «Winter»	16 м²
О12	стены	окраска, Farrow & Ball Modern Emulsion, матовая, подготовка Q3	Farrow & Ball No. 241 «Skimming Stone»	5,7 м²
О14	плинтус	плинтус МДФ, Orac Decor Contour (Luxxus), h 69 мм, SX165	Farrow & Ball No. 241 «Skimming Stone»	2,2 м


Ведомость точек и выводов

Марка	Что это	Гр.	H, мм	От угла, мм	Примечание
S4	выключатель	1	900	1785	

Ведомость изделий и проёмов (на листе)

Марка	Изделие, проём	На виде Ш×В, мм	Низ, мм
ДК4	зеркало	600×1600	300
Д-2	дверь скрытого монтажа	800×2100	0

Схема развёрток (М 1:50)

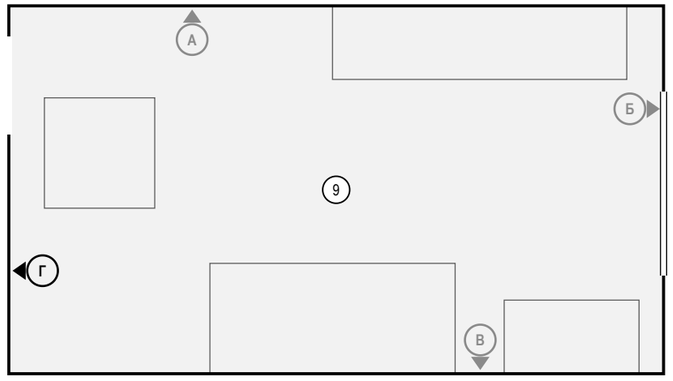

Примечания

1. Размеры — в мм от чистовых поверхностей стен; условные обозначения и общие указания — лист 14.
2. Картины и зеркала крепить к основанию по паспорту изделия (закладные и анкеры — в перечне скрытых работ); крест — ось центра предмета.
3. Двери скрытого монтажа — полотно в плоскости стены, отделка стены по полотну, плинтус прерывается у короба (узел — на листе узлов).
4. Потолок — у каждой стены свой, по плану потолков (ПТ3); ступени — зоной, кромка короба перед нишей — тонкой линией; в поле потолка: ПТ1 +2,600.

	Лист	№ док.	Подпись	Дата
Дизайнер	Кырлан А.С.			14.11.26
Проверил				
Н. контр.				
Утв.				

Проект: Квартира 65 м² — **М 1:20**

Развёртка стены Г. Детская (пом. 9)

Стадия	Лист	Листов
П	80	105

выпуск 14.11.2026 № 3aed0ef730 · стр. 80 из 105

Комплект предварительный по пунктам этих таблиц. Пока по пункту нет ответа или решения, показанное на указанном листе — допущение проектировщика, а не утверждённое решение.
Сводка: открытых вопросов — 12 (из них ждут факта объекта — 5: контрольного обмера, обследования или документа); изменений в реестре — 5, из них без подписи — 2.

Открытые вопросы и принятые допущения

№	Формулировка	Вид	Кто решает	Если решения нет	Лист, где это проявляется
К-1	Размеры квартиры сняты с растрового плана заказчика без размерных цепочек: масштаб восстановлен по подписанным площадям помещений. До заказа мебели, дверей и материалов нужен контрольный обмер всех помещений и проёмов.	Отсутствует Ждёт: обмера	Архитектор-планировщик	размеры на листах — по плану заказчика, уточняются по месту; мебель на заказ и материалы по ним не заказывать	л. 16 — План планировки от заказчика л. 22 — План размещения мебели и оборудования
К-2	Высота потолка на плане заказчика не указана, принята 2700 мм.	Отсутствует	Архитектор-планировщик	высоты на развёртках и потолки — от 2700 мм, уточнить при обмере	л. 16 — План планировки от заказчика л. 40 — План потолков
К-4	Разрешённая мощность квартиры по ТУ неизвестна, принята 15 кВт.	Отсутствует	Инженер-электрик	щит и группы рассчитаны на 15 кВт; при меньших ТУ пересчёт	л. 43 — Однолинейная схема щита л. 46 — План розеток и электровыводов
К-5	Кухня-гостиная (пом. 3): диван М-07 2200 × 950 стоит в полосе 1400 мм между спальней и кухней — единственном проходе от двери из коридора в комнату; за спинкой остаётся щель 290 мм, в выпуске для заказчика это ошибка. Полоса годится только под проход и неглубокую мебель (до 700 мм). В основной части (2700 × 2900 мм) диван, обеденная группа на 4 места, рабочее место М-08 и кресло М-06 вместе с проходами не помещаются. Нужно решение по составу зоны: (1) диван в основную часть лицом к ТВ на стене Г, обеденный стол — в нишу у колонны М-13, рабочее место М-08 — в спальню или детскую; (2) диван двухместный 1600 мм у стены спальни в основной части; (3) вместо обеденной группы — барная стойка. До решения расстановка кухни-гостиной не годится для заказа мебели. Решение исполнителя (ИЗ-1, 30.10.2026, на утверждение автора): вариант 1 без переноса рабочего места — диван М-07 у стены А основной части (x 250…2450, y 1650…2600), обеденный стол М-05 перед ним (x 1100…2100, y 2800…3800), кресло М-06 у окна 2 (x 400…1150, y 3700…4450), ТВ остаётся на стене Г; полоса 1400 у спальни свободна под проход; части 2–4 помещения перекроены (кухонный ряд и ниша — одна часть) без изменения контура. Стыки частей ≥ 700 мм.	Спорно Ждёт: решения	Дизайнер интерьера	расстановка М-07, М-05, М-06 остаётся предложением со знаком «**»: мебель кухни-гостиной не заказывать до подписи ИЗ-1	л. 22 — План размещения мебели и оборудования
К-6	Спальня (пом. 2) без окна (К-3): приток не решён — бризер на внутренней стене Б не работает (нужно отверстие в наружной стене), а наружная стена А занята изголовьем кровати М-02 (бризер над кроватью — холодный поток на спящего). Радиатор Р-2 оставлен на стене Б у двери. После решения по окну: бризер или клапан — у окна, радиатор — под окно; если помещение станет нежилым приток не нужен.	Решение	Инженер ОВ	приток в спальню не обеспечен: на плане вентиляции «!» в графе притока; радиатор Р-2 — на стене Б	л. 51 — План вентиляции л. 52 — План отопления
К-7	Вентканалы на плане заказчика не показаны: ВК-1 и ВК-2 приняты проектировщиком у кухни, ванная (пом. 7) от них далеко вытяжка ВР3 идёт воздуховодом ≈ 4 м через санузел. Замерить положение и сечение каналов; если канал у ванной есть — решётку в его стенку, воздуховод не нужен.	Отсутствует Ждёт: обмера	Инженер ОВ	вытяжка ванной — вентилятором с обратным клапаном и воздуховодом под потолком до ВК-2; места решёток — до обмера	л. 51 — План вентиляции
К-8	Проём санузла (пом. 6, марка Д-5) по плану заказчика 550×2100 — уже ряда стандартных полотен (600–900): полотно ≈ 450 под заказ, проход меньше 600. Откос от угла коридора до проёма — 40 мм, под коробку нужно не меньше 50. Проём в существующей стене: расширить до 700 (полотно 600) можно только при подтверждении, что стена не несущая (техзаключение / план БТИ). Замерить проём в чистоте и откос; решить — расширение по техзаключению или изделие под заказ.	Спорно Ждёт: обмера, затем решения	Архитектор-планировщик	Д-5 — скрытая дверь под заказ по проёму 550×2100 (полотно ≈ 450), проём не расширяется; заказ — только после замера в чистоте	л. 38 — План размещения дверей
К-9	Климатический подрайон (СП 131.13330) не задан: принят не северный — жилые комнаты и кухня под потолком от 2,5 м (СП 54, п. 5.12); в IA, IБ, IГ, IД, IVA — от 2,7 м.	Отсутствует Ждёт: документа	Архитектор-планировщик	отметки потолков жилых — по 2,5 м; при северном подрайоне уровни ниже 2,7 м пересчитать до заказа каркаса	л. 40 — План потолков
К-10	Несущие стены не определены: плана БТИ, проекта дома и технического заключения в материалах объекта нет. До их получения все существующие стены считаются несущими — демонтаж, новые проёмы и штробы в них не планируются. Нужно: запросить план БТИ и проект дома, установить серию и материал стен; несущие стены и допустимость вмешательства определяет техническое заключение специализированной организации.	Отсутствует Ждёт: документа	Архитектор-планировщик	все существующие стены — несущие: перепланировка и штробы в них не выполняются, на листах обмера и демонтажа — «не определены, считать несущими»	л. 16 — План планировки от заказчика полный альбом
К-12	Циркуляция ГВС в данных не задана — циркуляционного трубопровода на схеме нет. Решить: нужна ли циркуляция	Отсутствует Ждёт: решения	Инженер ВК (вода, канализация)	циркуляции на схеме нет	л. 32–34 — Развёртки мокрых зон: выводы ВК. Кухня-гостиная л. 29 — Аксонометрическая схема В1 (холодное водоснабжение) л. 28 — Схема разводки водопровода и канализации
К-13	Помещение «Гардеробная»: выключатель основного света L6 (S1) не у входа — у двери Д-3 со стороны ручки свободного места нет (проём в 100 мм от угла, мебель у двери, чужие точки или выключатель общий с соседним помещением; расстановка мебель и двери не двигает). Варианты: (а) петли на другую сторону — ручка уходит от угла, выключатель встаёт у ручки; (б) шкаф или тумбу у двери сдвинуть на 300 мм — место освобождается; (в) беспроводной выключатель на клее у ручки (реле в подрозетнике ближней стены) — по согласованию с заказчиком; (г) оставить как есть (S1): рука дальше 350 мм от ручки.	Спорно Ждёт: решения	Инженер-электрик	выключатель L6 остаётся на месте (S1); закладные под выключатель у двери не делать до решения	л. 50 — Управление светильниками

	Лист	№ док.	Подпись	Дата	Проект: Квартира 65 м²			
Дизайнер	Кырлан А.С.			14.11.26	Открытые вопросы, принятые допущения и конфликты. Лист 1 из 2	Стадия	Лист	Листов
Проверил						П	81	105
Н. контр.								
Утв.								

выпуск 14.11.2026 № 3aed0ef730 · стр. 81 из 105

Открытые вопросы и принятые допущения (продолжение)

№	Формулировка	Вид	Кто решает	Если решения нет	Лист, где это проявляется
К-14	Помещение «Коридор»: выключатель основного света L3 (S3, S5) не у входа — у двери А 150, Д-2, Д-2, Д-5, Д-4 со стороны ручки свободного места нет (проём в 100 мм от угла, мебель у двери, чужие точки или выключатель общий с соседним помещением; расстановка мебель и двери не двигает). Варианты: (а) петли на другую сторону — ручка уходит от угла, выключатель встаёт у ручки; (б) шкаф или тумбу у двери сдвинуть на 300 мм — место освобождается; (в) беспроводной выключатель на клее у ручки (реле в подрозетнике ближней стены) — по согласованию с заказчиком; (г) оставить как есть (S3, S5): рука дальше 350 мм от ручки.	Спорно Ждёт: решения	Инженер-электрик	выключатель L3 остаётся на месте (S3, S5); закладные под выключатель у двери не делать до решения	л. 50 — Управление светильниками

Изменения проекта после выпуска листов (реестр изменений)


№	Дата	Лист	Было	Стало	Кто решил, подпись
ИЗ-1	30.10.2026	л. 22 — План размещения мебели и оборудования л. 23 — Спецификация мебели и оборудования л. 46 — План розеток и электровыводов л. 61 — Развёртка стены В2. Кухня-гостиная (пом. 3), кухонный фронт	Кухня-гостиная (пом. 3): диван М-07 2200×950 стоял в полосе 1400 мм между спальней и кухней (x 2900…5100, y 3000…3950) — единственном проходе от двери Д-2; стыки частей 0–1 — 290 мм, 1–3 — 200, 1–4 — 0, 2–3 — 600; кресло М-06 в x 800, стол М-05 в x 1000, y 2700. Вопрос К-5 открыт.	Диван М-07 у стены А основной части (x 250…2450, y 1650…2600), стол М-05 перед ним (x 1100…2100, y 2800…3800), кресло М-06 у окна 2 (x 400…1150, y 3700…4450); розетки «у дивана» перенесены на стену А (x 700, 2300), розетка торшера — на стену Г (смещение 1900). Части помещения 2–4 перекроены без изменения контура: кухонный ряд М-09, М-10, М-11, М-12, М-13 и ниша М-08 — одна часть (0…4850 × 4550…5800), связка 2700…4850 × 4050…4550; стык частей 2–3 проходил сквозь кухонный ряд (600 мм — глубина столешницы, не проход). Знак «**» у М-07, М-05, М-06 до подписи автора; К-5 — у автора.	Утверждено: Кырлан А.С., 12.11.2026. Предложил: исполнитель.
ИЗ-2	10.11.2026	л. 22 — План размещения мебели и оборудования л. 46 — План розеток и электровыводов	Диван М-07 стоял на y 1700 мм, а чистая грань стены А помещения — на y 1710; розетка «у дивана» на стене А (смещение 200 мм, высота 300) — в 50 мм от бока дивана (x 250), закрыта мебелью.	Диван М-07 — у 1710 мм (было 1700), по чистой грани стены А: x 250…2450, y 1710…2660; размеры 2200 × 950 мм и положение по x прежние. Розетка «у дивана» на стене А — смещение 150 мм (было 200), высота 300 мм прежняя: 100 мм до бока дивана, 150 мм до угла. Вторая розетка у дивана (смещение 2550) не тронута. Диван остаётся предложением (ИЗ-1, К-5).	Утверждено: Кырлан А.С., 12.11.2026. Предложил: исполнитель.
ИЗ-3	11.11.2026	л. 16 — План планировки от заказчика л. 38 — План размещения дверей л. 58 — Развёртка стены А. Спальня (пом. 2) л. 22 — План размещения мебели и оборудования л. 46 — План розеток и электровыводов	Спальня (пом. 2, x 2700…6000, y 0…2650) выходила на наружную стену А (фасад, y = 0, как гардеробная и верхний край контура), но окна в ней не было: жилая комната без естественного освещения.	В наружной стене А спальни добавлено окно: смещение от левого угла стены 1400 мм, ширина 1400, высота 1600, подоконник 800 (тот же тип и размеры по высоте, что у окон кухни-гостиной и детской). Проём 1400…2800 лежит над изголовьем кровати М-02 (850…2450) и тумбой М-03 не задевает; бра L8 (смещения 1025 и 3150), розетки (1050, 3150) и выключатель S6 (1250) остаются вне проёма. Радиатор Р-2 остаётся на стене Б (под изголовьем кровати радиатор не ставится). Мебель не двигалась. Вопрос К-3 закрыт; приток воздуха (К-6) теперь решается клапаном или бризером в наружной стене рядом с окном, после обмера и утверждения.	Утверждено: Кырлан А.С., 12.11.2026. Предложил: исполнитель.
ИЗ-4	12.11.2026	полный альбом	Декор и текстиль были заданы только в детской (пом. 9). В кухне-гостиной, спальне, прихожей, коридоре и санузлах не было ни штор, ни ковров, ни подушек и пледов, ни картин, зеркал и растений; кадры визуализаций и листы декоратора строятся только по данным — помещения выходили пустыми. В детской подушки и плед (Т10–Т12) были записаны «на М-21» (это стол), у картины ДК3 не было сюжета.	Декор и текстиль заданы позициями плана. Кухня-гостиная: римские шторы на оба окна (Т1, Т2; в пол не идут — под окнами радиаторы, диван в 250 мм от окна 1), подушки 3 + 2 и плед на диван М-07 (Т3–Т5), картина 1400×900 над диваном на стене А (ДК1; низ 1050), сансевиерия в напольном кашпо у рабочего места (ДК2), ваза на обеденном столе М-05 (ДК5). Спальня: римская штора с блэкаутом на окно над изголовьем (Т6), ковёр 2500×1250 под кроватью с выходом по 450 мм по бокам, вне зоны открывания двери Д-3 (Т13), подушки 2 + 1 и плед на кровать М-02 (Т14–Т16), картина 1000×700 на стене В напротив кровати (ДК6), зеркало в рост 500×1600 на стене Г у двери гардеробной (ДК7). Прихожая: дорожка 800×1400 (Т17), зеркало в рост 500×1600 на стене Г (ДК8). Коридор: три постера 400×560 в дубовых рамах на глухой стене А, шаг между рамами 70 мм (ДК9–ДК11). Санузел и ванная: зеркала над умывальниками С-03 и С-05 (ДК12, ДК13). Детская: подушки и плед Т10–Т12 — на кровать М-20 (было «М-21» — стол), картине ДК3 задан сюжет. Цвета — из палитры стиля: молочный, каменный, акценты — приглушённый синий Farrow & Ball No. 299 и терракота NCS S 3020-Y80R. Ковёр в кухне-гостиной не задан: обеденный стол М-05 стоит в 140 мм от дивана, ковёр под столом с выходом 600 мм не помещается; дорожка в коридоре не задана — пол в зонах открывания четырёх дверей. Знак «**» у позиций до подписи автора.	Не утверждено: подписи нет. решение исполнителя; предложение проектировщика, на утверждение А. С. Кырлана
ИЗ-5	12.11.2026	полный альбом	Разбор двух критиков по кадрам: мокрые зоны — «стерильный шоурум»: в ванной на полотенцесушителе С-06 нет полотенец, у ванны нет коврика; в санузле, кроме зеркала, ничего нет (ИЗ-4 задал там только зеркала). Замечание «ванна без смесителя» по данным не подтверждается: у С-04 записано «смеситель настенный» — это расхождение кадра, а не данных.	Ванная: банные полотенца приглушённого синего и ручные молочные на полотенцесушителе С-06 (Т18, Т19), коврик 600×450 у бортика ванны (Т20; вне полотна двери Д-4 и перед умывальником С-05). Санузел: постер 300×400 на стене Г (ДК14); полки короба инсталляции в данных санузла нет — предметы на полку не заданы. Прихожая и коридор не дополнялись: зеркало, дорожка и триптих заданы ИЗ-4, свободных простенков нет. Знак «**» у позиций до подписи автора.	Не утверждено: подписи нет. решение исполнителя; предложение проектировщика, на утверждение А. С. Кырлана

Примечания


1. Номера листов — по ведомости рабочих чертежей комплекта (лист «Общие данные»).
2. Графа «Если решения нет» показывает состояние решения на листах; влияние на сроки и стоимость по пунктам не оценивалось.
3. Пункт, по которому принято решение, при следующем выпуске комплекта из таблиц исключается.

	Лист	№ док.	Подпись	Дата	Проект: Квартира 65 м²			
Дизайнер	Кырлан А.С.			14.11.26	Открытые вопросы, принятые допущения и конфликты. Лист 2 из 2	Стадия	Лист	Листов
Проверил						П	82	105
Н. контр.								
Утв.								


Общий вид (М 1:40)

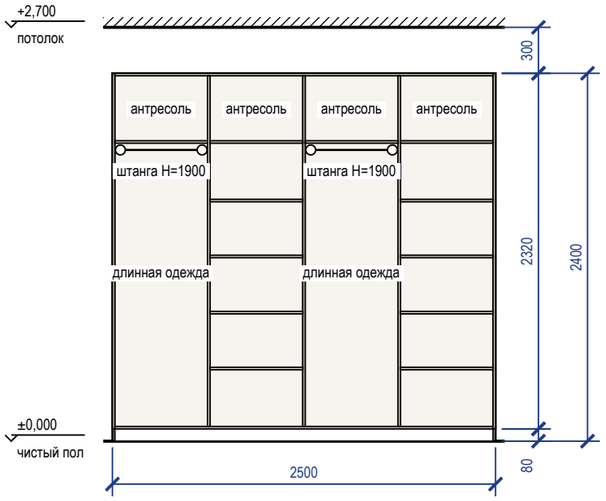


Наполнение, размеры в свету (М 1:40)

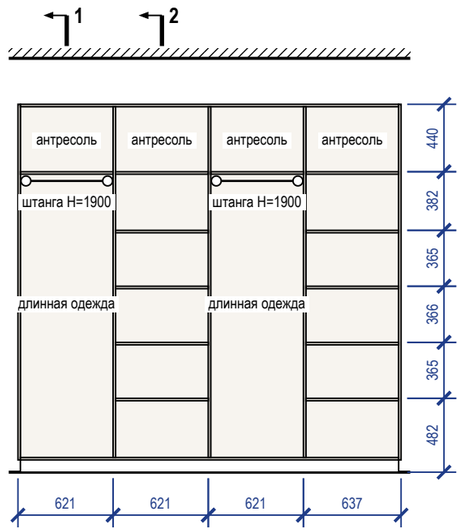

Разрез 1-1 (М 1:40)

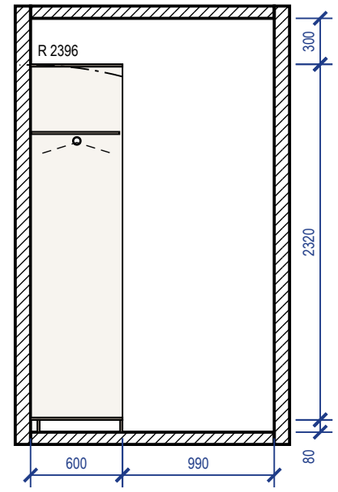


Разрез 2-2 (М 1:40)

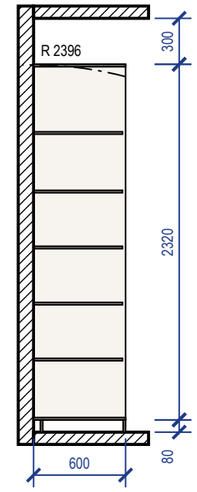

Примечания

1. Размеры — в мм по чистовой отделке; изделие 2500×600×2400 (Ш×Г×В). Перед раскроем — контрольный замер цеха после чистовой отделки стен, пола и потолка.
2. Корпус — ЛДСП 16 мм, задняя стенка ХДФ 4 мм в паз, цоколь 80 мм на регулируемых опорах; открытая система: без фасадов.
3. Кромка: скрытые торцы 0,4 мм, видимые 2 мм (ПВХ/АБС).
4. Присадка по 32-й системе — выполняет цех.
5. Зазор до потолка 300 мм.
6. Подъём корпуса: диагональ боковины без цоколя $\sqrt{(2320^2 + 600^2)}$ = 2396 мм < 2700 мм до потолка — корпус собирается лёжа, поднимается поворотом и ставится на цоколь.
7. Крепление к стене от опрокидывания: крепление к стене, 3 точки; основание стены и шаг анкеров — монтажная схема шкафов.
8. Проход перед изделием 990 мм показан на разрезе 1-1.

3D орто

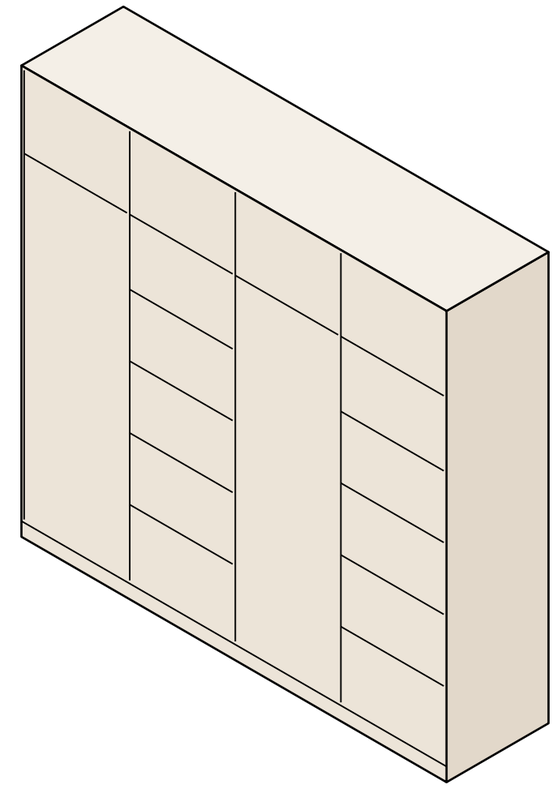


	Лист	№ док.	Подпись	Дата
Дизайнер	Кырлан А.С.			14.11.26
Проверил				
Н. контр.				
Утв.				

Проект: Квартира 65 м² — **М 1:40**


Система хранения М-01	Стадия	Лист	Листов
	П	Д1	105

выпуск 14.11.2026 № 3aed0ef730 · стр. 83 из 105


Вид с фасадами (М 1:20)

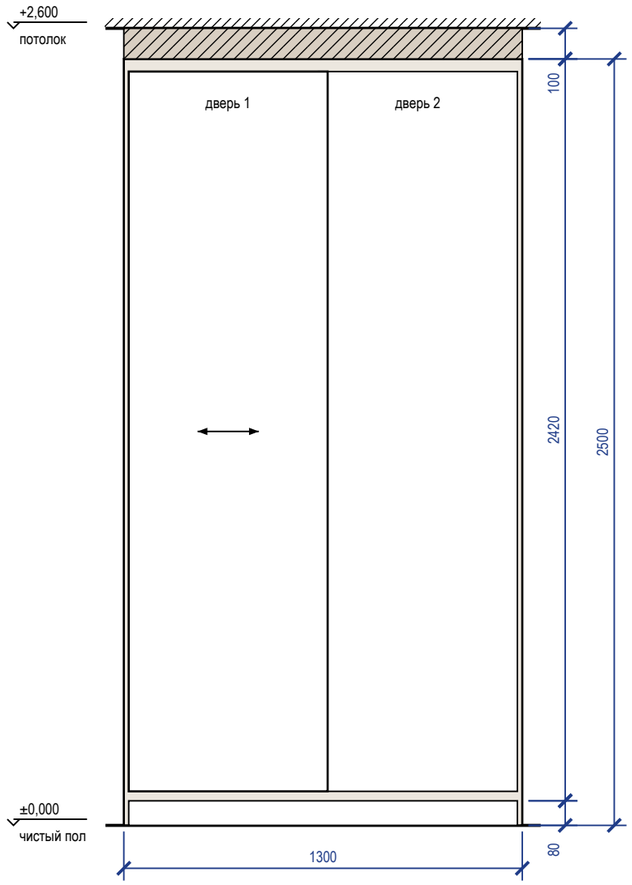


Вид без фасадов (М 1:20)

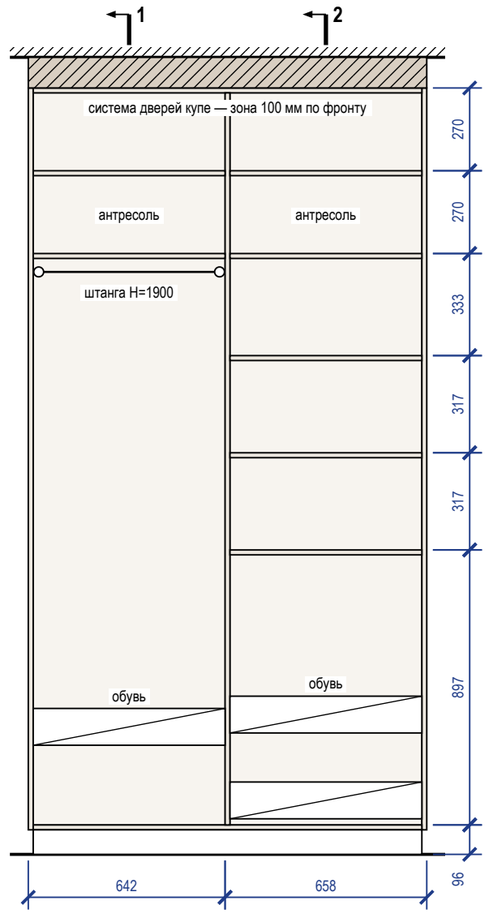

Разрез 1-1 (М 1:20)

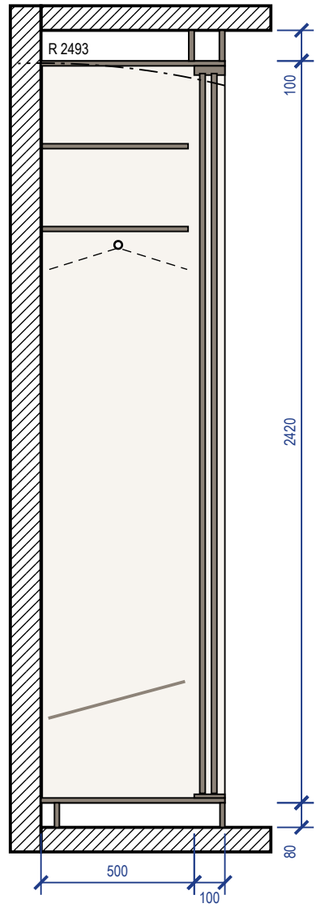


Разрез 2-2 (М 1:20)

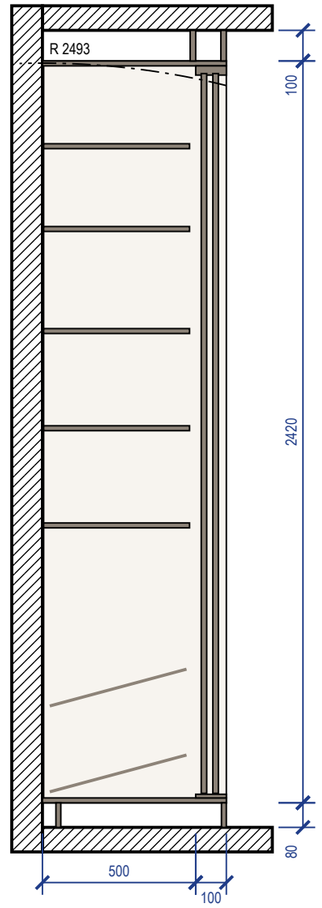

Примечания

1. Размеры — в мм по чистовой отделке; изделие 1300×600×2500 (Ш×Г×В). Перед раскроем — контрольный замер цеха после чистовой отделки стен, пола и потолка.
2. Корпус — ЛДСП 16 мм, задняя стенка ХДФ 4 мм в паз, цоколь 80 мм на регулируемых опорах; двери купе — ЛДСП 10 мм в алюминиевом профиле; нахлёст 30 мм, ширина двери 649 мм, высота — проём минус 40 мм; цвет — по колерной карте.
3. Кромка: скрытые торцы 0,4 мм, видимые 1 мм (ПВХ/АБС).
4. Номинальные зазоры: дверь купе — боковина 3 мм, фасад ящика — стойка 2 мм; ящики внутри купе — с накладкой 30 мм на стойке со стороны нахлёста дверей.
5. Присадка по 32-й системе — выполняет цех.
6. Компенсатор 100 мм — короб из ЛДСП по фронту и торцам, подгоняется к потолку при монтаже (припуск 20 мм), крепится к корпусу и к потолку.
7. Подъём корпуса: диагональ боковины без цоколя $\sqrt{(2420^2 + 600^2)} = 2493$ мм < 2600 мм до потолка — корпус собирается лёжа, поднимается поворотом и ставится на цоколь.
8. Крепление к стене от опрокидывания — уголки 2 шт. к несущему основанию (монтажная схема шкафов).


3D орто

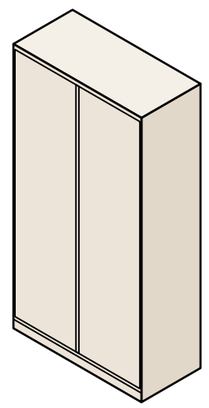


	Лист	№ док.	Подпись	Дата	Проект: Квартира 65 м²			М 1:20
Дизайнер	Кырлан А.С.			14.11.26	Шкаф-купе М-17	Стадия	Лист	Листов
Проверил						П	Д2	105
Н. контр.								
Утв.								

выпуск 14.11.2026 № 3aed0ef730 · стр. 84 из 105


Общий вид (М 1:20)

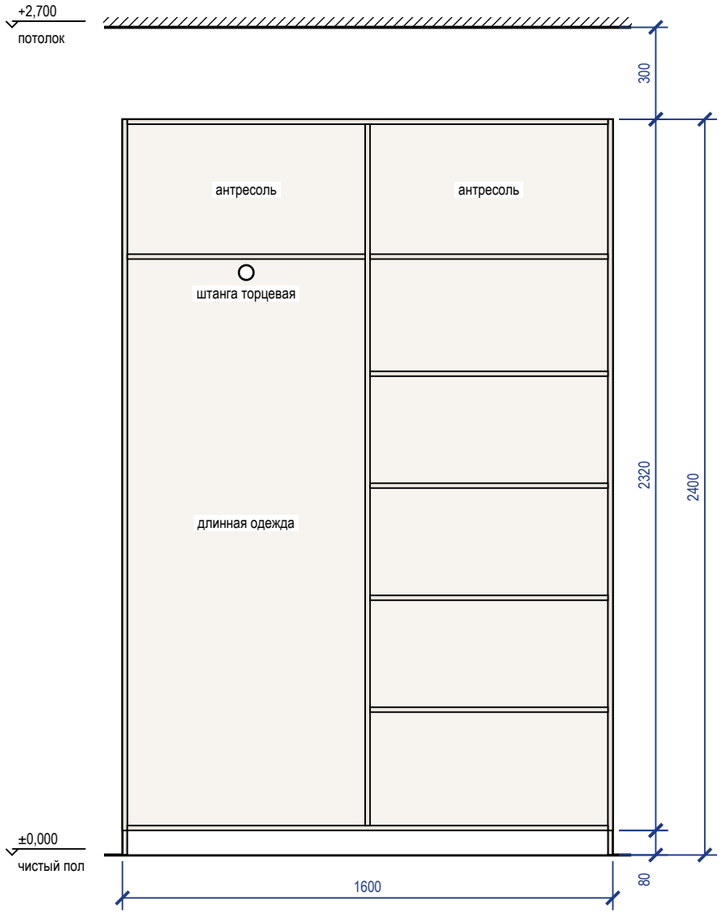


Наполнение, размеры в свету (М 1:20)

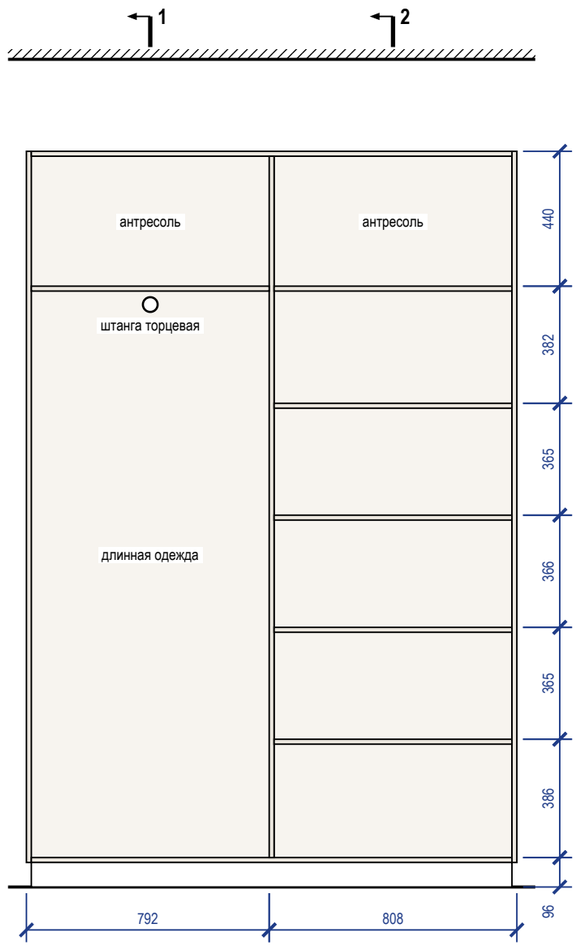

Разрез 1-1 (М 1:20)

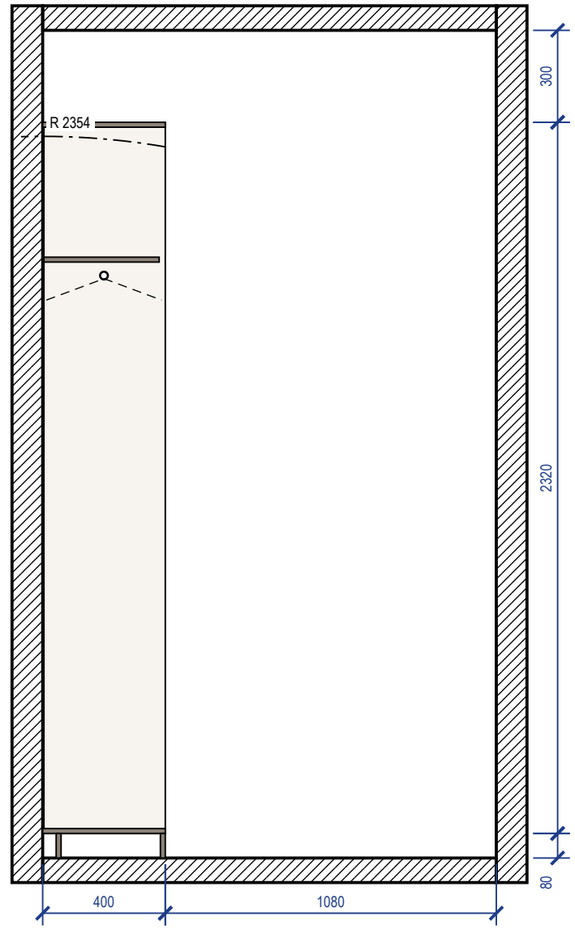


Разрез 2-2 (М 1:20)

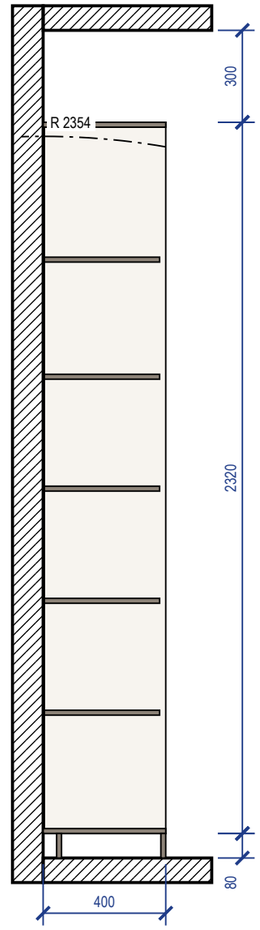

Примечания

1. Размеры — в мм по чистовой отделке; изделие 1600×400×2400 (Ш×Г×В). Перед раскроем — контрольный замер цеха после чистовой отделки стен, пола и потолка.
2. Корпус — ЛДСП 16 мм, задняя стенка ХДФ 4 мм в паз, цоколь 80 мм на регулируемых опорах; открытая система: без фасадов.
3. Кромка: скрытые торцы 0,4 мм, видимые 2 мм (ПВХ/АБС).
4. Присадка по 32-й системе — выполняет цех.
5. Зазор до потолка 300 мм.
6. Подъём корпуса: диагональ боковины без цоколя √(2320² + 400²) = 2354 мм < 2700 мм до потолка — корпус собирается лёжа, поднимается поворотом и ставится на цоколь.
7. Крепление к стене от опрокидывания — уголки 2 шт. к несущему основанию (монтажная схема шкафов).
8. Проход перед изделием 1080 мм показан на разрезе 1-1.

3D орто

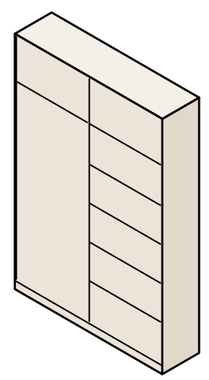


	Лист	№ док.	Подпись	Дата
Дизайнер	Кырлан А.С.			14.11.26
Проверил				
Н. контр.				
Утв.				

Проект: Квартира 65 м² — **М 1:20**


Система хранения М-18

Стадия	Лист	Листов
П	Д3	105


Вид с фасадами (М 1:25)

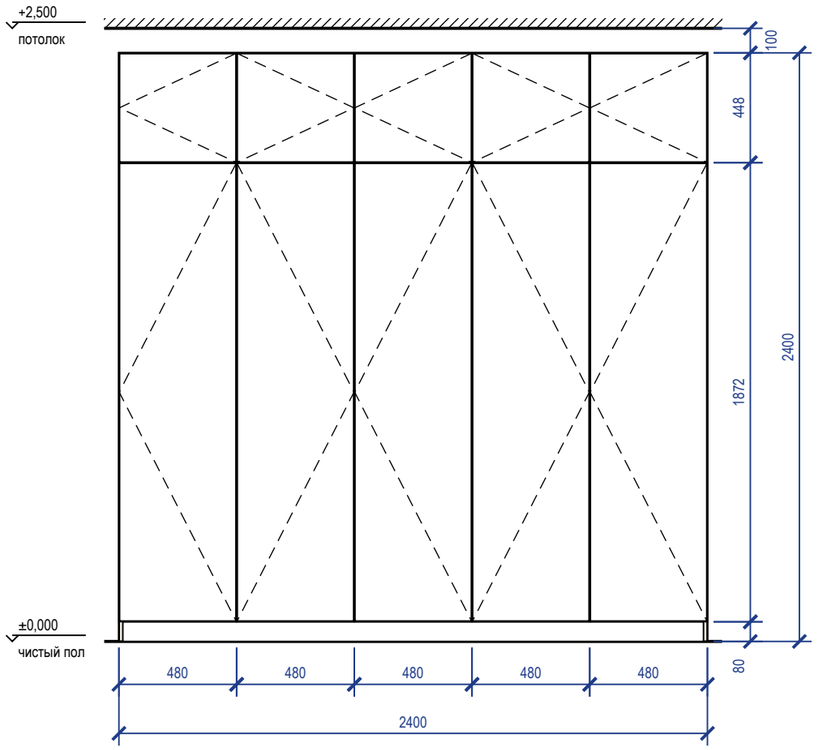


Вид без фасадов (М 1:25)

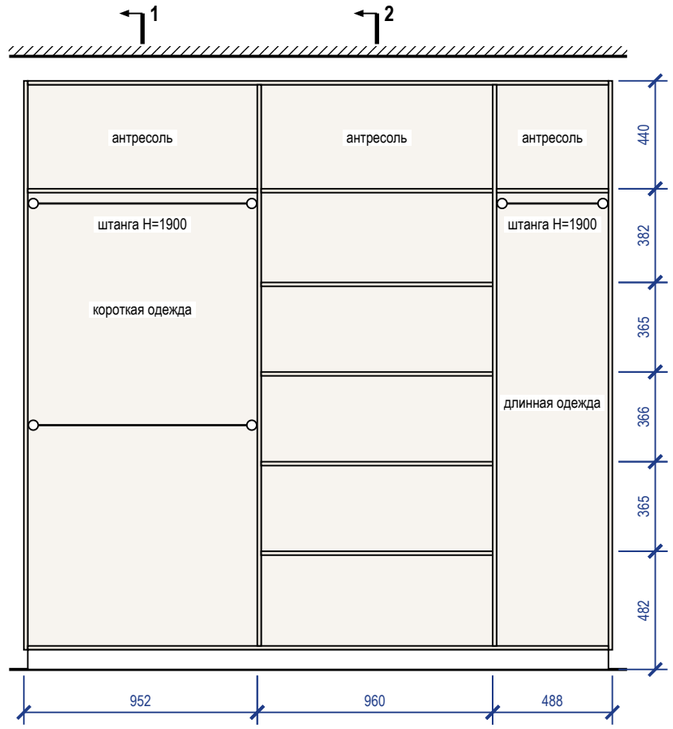

Разрез 1-1 (М 1:25)

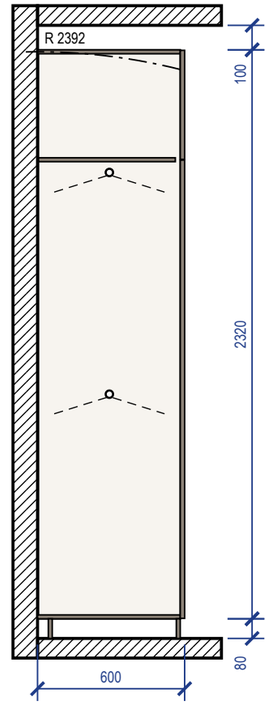


Разрез 2-2 (М 1:25)

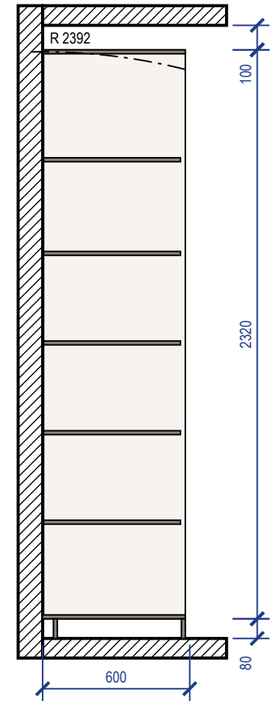

Примечания

1. Размеры — в мм по чистовой отделке; изделие 2400×600×2400 (Ш×Г×В). Перед раскроем — контрольный замер цеха после чистовой отделки стен, пола и потолка.
2. Корпус — ЛДСП 16 мм, задняя стенка ХДФ 4 мм в паз, цоколь 80 мм на регулируемых опорах; фасады накладные — МДФ 18 мм, эмаль матовая, 18 мм; цвет — по колерной карте; петли с доводчиком: фасад 1869 мм — 4 петли, фасад 445 мм — 2 петли.
3. Кромка: скрытые торцы 0,4 мм, видимые 2 мм (ПВХ/АБС).
4. Номинальные зазоры: между фасадами 3 мм, фасад — стена и фасад — потолок не менее 3 мм, фасад ящика — стойка 2 мм.
5. Присадка по 32-й системе — выполняет цех.
6. Зазор до потолка 100 мм — закрыть планкой в цвет корпуса при монтаже.
7. Подъём корпуса: диагональ боковины без цоколя √(2320² + 582²) = 2392 мм < 2500 мм до потолка — корпус собирается лёжа, поднимается поворотом и ставится на цоколь.
8. Крепление к стене от опрокидывания — уголки 2 шт. к несущему основанию (монтажная схема шкафов).

3D орто

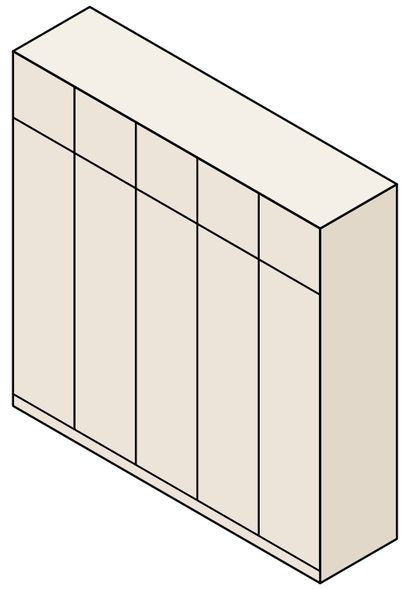

	Лист	№ док.	Подпись	Дата
Дизайнер	Кырлан А.С.			14.11.26
Проверил				
Н. контр.				
Утв.				


Проект: Квартира 65 м² — **М 1:25**

Шкаф распашной М-19


Стадия	Лист	Листов
П	Д4	105

выпуск 14.11.2026 № 3aed0ef730 · стр. 86 из 105


Вид с фасадами (М 1:25)

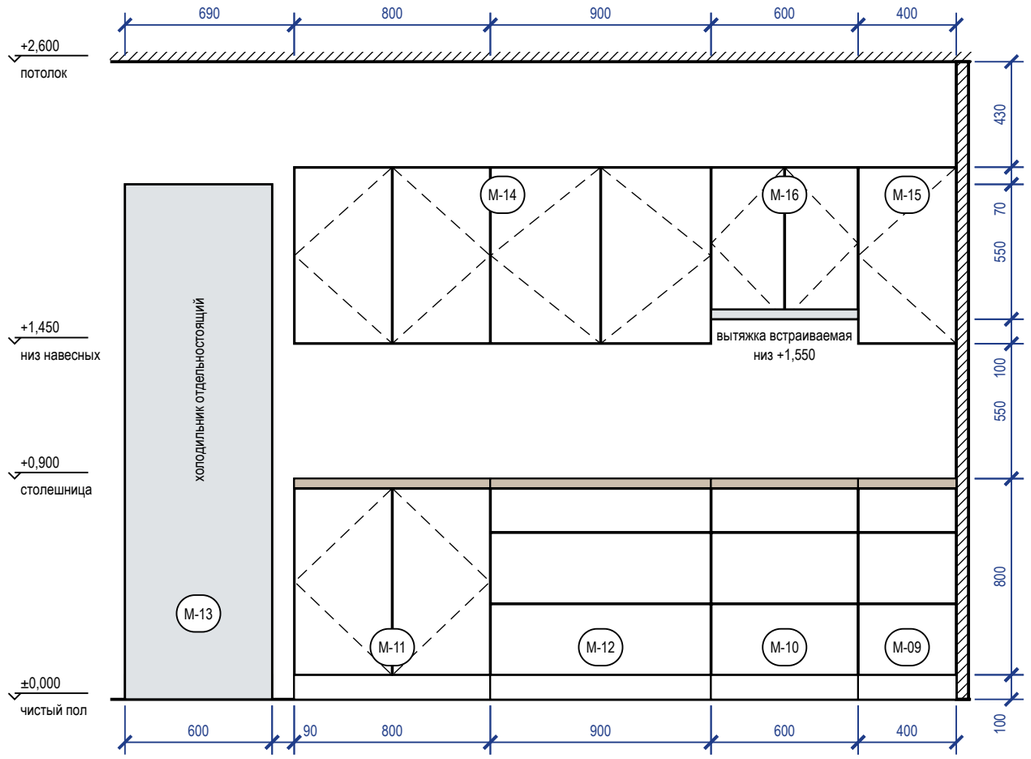


Вид без фасадов: наполнение, выводы (М 1:25)

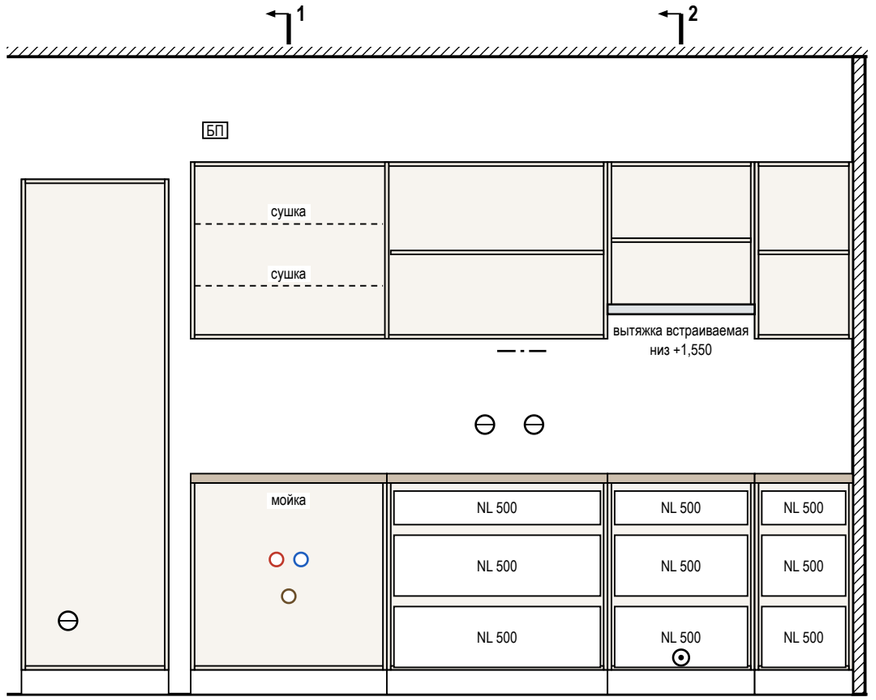


Разрез 1-1 (М 1:25)

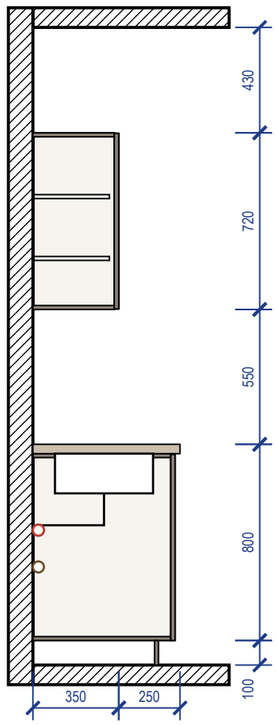

Разрез 2-2 (М 1:25)

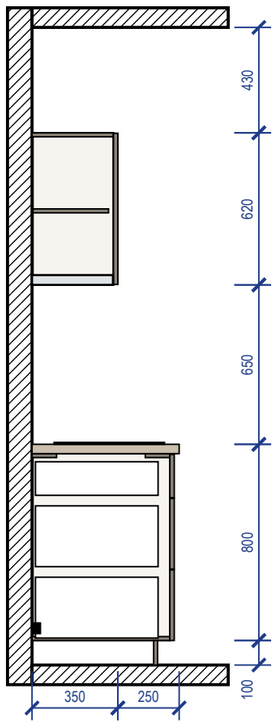

3D орто

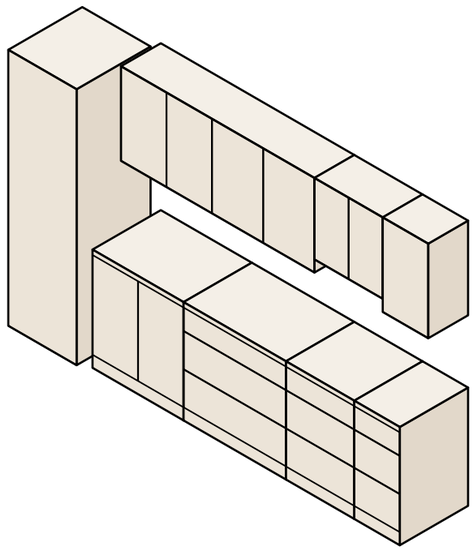

Примечания

1. Размеры — в мм по чистовой отделке, вид из помещения; марки — как на плане расстановки. Перед раскроем — контрольный замер цеха после фартука и пола.
2. Корпуса — ЛДСП 16 мм, задняя стенка ХДФ 4 мм; фасады — МДФ эмаль 18 мм, цвет по колерной карте; столешница 38 мм, свес 20 мм; цоколь 100 мм.
3. Кромка: скрытые торцы 0,4 мм, видимые 1 мм. Номинальные зазоры: между фасадами 3 мм, фасад — столешница 3 мм, фасад — стена не менее 3 мм.
4. Ящики полного выдвижения и петли — с доводчиком; присадка по 32-й системе — выполняет цех.
5. Наименования и габариты модулей (М…) — в ведомости изделий, лист 26.
6. Вытяжка встраивается в дно навесного модуля М-16 над варочной: её низ на 1550 мм от пола, 650 мм над панелью (не меньше 650 мм).
7. Ниши техники — по монтажным схемам выбранных моделей: решётка в цоколе и канал за пеналом холодильника, зазор за духовым шкафом, фасад ПММ на двери машины.

	Лист	№ док.	Подпись	Дата	Проект: Квартира 65 м²			М 1:25
Дизайнер	Кырлан А.С.			14.11.26	Кухня (пом. 3). Развёртка гарнитура	Стадия	Лист	Листов
Проверил						П	Д5	105
Н. контр.								
Утв.								

Ведомость отделки помещений (форма 1 прил. А ГОСТ 21.501-2018)

№	Наименование помещения	Потолок			Стены и перегородки			Низ стен (плинтус)			Пол		Примечание
		Вид отделки	Код цвета	S, м²	Вид отделки	Код цвета	S, м²	Вид отделки	Код цвета	L, м	Вид отделки	S, м²	
1	Гардеробная 4,20 м²	Существующий потолок, отм. +2,700; окраска, Tikkurila Anti-Reflex 2, глубокоматовая, 2 слоя, подготовка Q3	Tikkurila V503	4,20	Окраска, Tikkurila Harmony, матовая, 2 слоя, подготовка Q3	Tikkurila V503	21,37	Плинтус МДФ h=69 мм, SX165	Tikkurila V503	7,8	Инженерная доска, 1167-1101, 2100×127 мм, на клею; тип 1, отм. ЧП ±0,000	4,20	Н стен 2700 (до потолка); плинтус в цвет: стены
2	Спальня 8,27 м²	ГКЛ по каркасу П113, отм. +2,600; окраска, Tikkurila, глубокоматовая	NCS S 0300-N	8,27	Окраска, Tikkurila, глубокоматовая, подготовка Q3	NCS S 1502-Y50R	25,14	Плинтус МДФ h=69 мм, SX165	NCS S 0300-N	10,3	Инженерная доска, 1167-1101, 2100×127 мм, на клею; тип 1, отм. ЧП ±0,000	8,27	Н стен 2600 (до потолка)
3	Кухня-гостиная 18,91 м²	ГКЛ по каркасу П113, отм. +2,600; окраска, Tikkurila, глубокоматовая	NCS S 0300-N	18,91	Окраска, Tikkurila, полуматовая, подготовка Q3	NCS S 1002-Y50R	46,29	Плинтус МДФ h=69 мм, SX165	NCS S 0300-N	18,6	Инженерная доска, 1167-1101, 2100×127 мм, на клею; тип 1, отм. ЧП ±0,000	18,91	Н стен 2600 (до потолка)
4	Прихожая 4,15 м²	ГКЛ по каркасу П113, отм. +2,600; окраска, Tikkurila, глубокоматовая	NCS S 0300-N	4,15	Окраска, Tikkurila, полуматовая, подготовка Q3	NCS S 1502-Y50R	16,60	Плинтус МДФ h=69 мм, SX165	NCS S 0300-N	6,0	Керамогранит, SG501600R, 600×1200 мм; тип 2, отм. ЧП ±0,000	4,15	Н стен 2600 (до потолка)
5	Коридор 5,51 м²	ГКЛ по каркасу П113, отм. +2,600; окраска, Tikkurila, глубокоматовая	NCS S 0300-N	5,51	Окраска, Tikkurila, полуматовая, подготовка Q3	NCS S 1502-Y50R	20,60	Плинтус МДФ h=69 мм, SX165	NCS S 0300-N	7,0	Керамогранит, SG501600R, 600×1200 мм; тип 2, отм. ЧП ±0,000	5,51	Н стен 2600 (до потолка)
6	Санузел 1,83 м²	ГКЛВ по каркасу П113, отм. +2,600; окраска, Tikkurila, глубокоматовая	NCS S 0300-N	1,83	Облицовка плиткой, 610010001195, 600×1200 мм, клей С2	Italon 610010001195	13,33	нет (облицовка от пола)			Керамогранит, SG501600R, 600×1200 мм; тип 3, отм. ЧП −0,015	1,83	Н стен 2615 (до потолка); гидроизоляция обмазочная, 2 слоя, с заведением на стены 200 мм (по пирогу пола); тест проливом и акт скрытых работ
7	Ванная 3,85 м²	ГКЛВ по каркасу П113, отм. +2,600; окраска, Tikkurila, глубокоматовая	NCS S 0300-N	3,85	Облицовка плиткой, 610010001195, 600×1200 мм, клей С2	Italon 610010001195	19,29	нет (облицовка от пола)			Керамогранит, SG501600R, 600×1200 мм; тип 3, отм. ЧП −0,015	3,85	Н стен 2615 (до потолка); тёплый пол; гидроизоляция обмазочная, 2 слоя, с заведением на стены 200 мм; над ванной — до 2000 и 300 мм за борт (по пирогу пола); тест проливом и акт скрытых работ
8	Кладовая 2,50 м²	Существующий потолок, отм. +2,700; окраска, Tikkurila, глубокоматовая	NCS S 0300-N	2,50	Окраска, Tikkurila, матовая, подготовка Q3	NCS S 0502-Y	15,65	Плинтус МДФ h=69 мм, SX165	NCS S 0300-N	5,6	Инженерная доска, 1167-1101, 2100×127 мм, на клею; тип 1, отм. ЧП ±0,000	2,50	Н стен 2700 (до потолка)
9	Детская 16,02 м²	ГКЛ по каркасу П113, отм. +2,500; +2,600; окраска, Tikkurila Anti-Reflex 2, глубокоматовая, 2 слоя, подготовка Q3	Tikkurila V503	16,02	Окраска, Farrow & Ball Modern Emulsion, матовая, 2 слоя, подготовка Q3 Акцент — стена А: окраска, Farrow & Ball Modern Emulsion, матовая, 2 слоя, подготовка Q3	Farrow & Ball No. 241 Farrow & Ball No. 30	24,27 13,35	Плинтус МДФ h=69 мм, SX165	Farrow & Ball No. 241	15,9	Инженерная доска, 1167-1101, 2100×127 мм, на клею; тип 1, отм. ЧП ±0,000	16,02	Н стен 2500 (до потолка); плинтус в цвет: стены
	Итого			**65,24**			**215,88**			**71,1**		**65,24**	

Примечания

1. Площади поверхностей — по чистым граням стен до отделки: стены = периметр × высоту от чистого пола помещения до низа потолка минус проёмы (облицовка плиткой — до верха облицовки); плинтус = периметр минус дверные проёмы; пол и потолок — по площади помещения. Количество плиток по раскладке. Площади помещений — с учётом всех частей помещения; откосы в площадь стен не входят.
2. Акцентные стены — отдельными строками, их площадь вычтена из основной отделки стен помещения.
3. Плинтус — длина по периметру за вычетом дверных проёмов; примыкания к наличникам и встроенной мебели — по развёрткам.
4. Формат плитки — Ш×В×Т (ширина × высота в положении укладки × толщина), мм; на полу — вдоль стен А/В × вдоль стен Б/Г.
5. Коды цвета — по веерам производителей; колеровка каждой краски одной партией, проверка выкраса при свете D65 и при лампах проекта.
6. Уровни подготовки Q1–Q4 — система Knauf, не норма ГОСТ/СП; допуски поверхностей — по СП 71.13330.2017 (действующая редакция).
7. «аналог:» — изделие задано характеристиками, марку и артикул согласовать с заказчиком до закупки.
8. Сводка площадей по материалам, м²: потолок — Tikkurila V503 Anti-Reflex 2 — 20,22; потолок — NCS S 0300-N — 45,02; стены — Tikkurila V503 Harmony — 21,37; стены — NCS S 1502-Y50R — 62,33; стены — NCS S 1002-Y50R — 46,29; стены — облицовка плиткой 600×1200 мм, Italon 610010001195 — 32,63; стены — NCS S 0502-Y — 15,65; стены — Farrow & Ball No. 241 Modern Emulsion — 24,27; стены — Farrow & Ball No. 30 Modern Emulsion 13,35.

	Лист	№ док.	Подпись	Дата	Проект: Квартира 65 м²			
Дизайнер	Кырлан А.С.			14.11.26	Ведомость отделки помещений	Стадия	Лист	Листов
Проверил						П	С1	105
Н. контр.								
Утв.								

Поз.	Наименование и техническая характеристика	Тип, марка, обозначение документа	Код продукции	Поставщик	Ед. изм.	Кол.	Образец	Примечание
	Лакокрасочные материалы							
1	Краска интерьерная водно-дисперсионная акриловая для стен, матовая, класс мокрого истирания 1 по EN 13300, база A; цвет по вееру Tikkurila V503 «Winter», колеровка машинная	Tikkurila Harmony		Tikkurila	л	6,3		поз. К1 колерной карты; пом. 1; S = 21,4 м² × 2 сл. × 0,12 л/м² = 5,1 л, +10 % и 0,5 л на подкраску → ≥ 6,1 л; тара 2 × 2,7 л + 1 × 0,9 л
2	Краска интерьерная водно-дисперсионная акриловая для потолков, глубокоматовая, класс мокрого истирания 2 по EN 13300, база A; цвет по вееру Tikkurila V503 «Winter», колеровка машинная	Tikkurila Anti-Reflex 2		Tikkurila	л	6,3		поз. К2 колерной карты; пом. 1, 9; S = 20,2 м² × 2 сл. × 0,12 л/м² = 4,9 л, +10 % и 0,5 л на подкраску → ≥ 5,8 л; тара 2 × 2,7 л + 1 × 0,9 л
3	Краска интерьерная водно-дисперсионная акриловая для стен, глубокоматовая, класс мокрого истирания 2 по EN 13300, база A; цвет NCS S 1502-Y50R, колеровка машинная	Tikkurila		Tikkurila	л	7,2		поз. К4 колерной карты; пом. 2; S = 25,1 м² × 2 сл. × 0,12 л/м² = 6,0 л, +10 % и 0,5 л на подкраску → ≥ 7,1 л; тара 2 × 2,7 л + 2 × 0,9 л
4	Краска интерьерная водно-дисперсионная для потолков, глубокоматовая, класс мокрого истирания 2 по EN 13300, база A; цвет NCS S 0300-N, колеровка машинная	Tikkurila		Tikkurila	л	3,6		поз. К5 колерной карты; пом. 2, 8; S = 10,8 м² × 2 сл. × 0,12 л/м² = 2,6 л, +10 % и 0,5 л на подкраску → ≥ 3,3 л; тара 1 × 2,7 л + 1 × 0,9 л
5	Краска интерьерная водно-дисперсионная акриловая для стен, полуматовая, класс мокрого истирания 1 по EN 13300, база A; цвет NCS S 1002-Y50R, колеровка машинная	Tikkurila		Tikkurila	л	13,5		поз. К7 колерной карты; пом. 3; S = 46,3 м² × 2 сл. × 0,12 л/м² = 11,1 л, +10 % и 0,5 л на подкраску → ≥ 12,7 л; тара 1 × 9 л + 1 × 2,7 л + 2 × 0,9 л
6	Краска интерьерная водно-дисперсионная для потолков, глубокоматовая, класс мокрого истирания 1 по EN 13300, база A; цвет NCS S 0300-N, колеровка машинная	Tikkurila		Tikkurila	л	9,9		поз. К8 колерной карты; пом. 3, 4, 5, 6, 7; S = 34,3 м² × 2 сл. × 0,12 л/м² = 8,2 л, +10 % и 0,5 л на подкраску → ≥ 9,5 л; тара 1 × 9 л + 1 × 0,9 л
7	Краска интерьерная водно-дисперсионная акриловая для стен, полуматовая, класс мокрого истирания 1 по EN 13300, база A; цвет NCS S 1502-Y50R, колеровка машинная	Tikkurila		Tikkurila	л	10,8		поз. К9 колерной карты; пом. 4, 5; S = 37,2 м² × 2 сл. × 0,12 л/м² = 8,9 л, +10 % и 0,5 л на подкраску → ≥ 10,3 л; тара 1 × 9 л + 2 × 0,9 л
8	Краска интерьерная водно-дисперсионная акриловая для стен, матовая, класс мокрого истирания 2 по EN 13300, база A; цвет NCS S 0502-Y, колеровка машинная	Tikkurila		Tikkurila	л	5,4		поз. К10 колерной карты; пом. 8; S = 15,6 м² × 2 сл. × 0,12 л/м² = 3,8 л, +10 % и 0,5 л на подкраску → ≥ 4,6 л; тара 2 × 2,7 л
9	Краска интерьерная водно-дисперсионная акриловая для стен, матовая, класс мокрого истирания 1 по EN 13300, база A; цвет по вееру Farrow & Ball No. 241 «Skimming Stone», колеровка машинная	Farrow & Ball Modern Emulsion		Farrow & Ball	л	7,5		поз. К11 колерной карты; пом. 9; S = 24,3 м² × 2 сл. × 0,12 л/м² = 5,8 л, +10 % и 0,5 л на подкраску → ≥ 6,9 л; тара 1 × 5 л + 1 × 2,5 л
10	Краска интерьерная водно-дисперсионная акриловая для акцентных стен, матовая, класс мокрого истирания 1 по EN 13300, база C; цвет по вееру Farrow & Ball No. 30 «Hague Blue», колеровка машинная	Farrow & Ball Modern Emulsion		Farrow & Ball	л	5		поз. К12 колерной карты; пом. 9; S = 13,3 м² × 2 сл. × 0,12 л/м² = 3,2 л, +10 % и 0,5 л на подкраску → ≥ 4,0 л; тара 1 × 5 л
11	Краска для МДФ и дерева в цвет Tikkurila V503 «Winter» — окраска плинтуса; блеск не ниже блеска стен	марка не задана			л	0,5		поз. К3; пом. 1; L = 7,8 м, S = 0,7 м² × 2 сл. × 0,12 л/м² + 10 %; продукт подобрать в веере Tikkurila
12	Акрил, полуматовая в цвет NCS S 0300-N — окраска плинтуса	аналог по характеристикам			л	1,1		поз. К6; пом. 2, 3, 4, 5, 8; L = 47,4 м, S = 4,0 м² × 2 сл. × 0,12 л/м² + 10 %; продукт подобрать в веере NCS
13	Краска для МДФ и дерева в цвет Farrow & Ball No. 241 «Skimming Stone» — окраска плинтуса; блеск не ниже блеска стен	марка не задана			л	0,5		поз. К13; пом. 9; L = 15,9 м, S = 1,3 м² × 2 сл. × 0,12 л/м² + 10 %; продукт подобрать в веере Farrow & Ball
14	Грунтовка акриловая под окраску стен и потолков — из системы производителя краски	по системе краски			м²	249		площадь окраски стен, акцентов и потолков; 1 слой перед окраской; расход — по ТУ грунтовки

	Лист	№ док.	Подпись	Дата
Дизайнер	Кырлан А.С.			14.11.26
Проверил				
Н. контр.				
Утв.				

Проект: Квартира 65 м²

Спецификация отделочных материалов	Стадия	Лист	Листов
	П	С2	105

выпуск 14.11.2026 № 3aed0ef730 · стр. 89 из 105

Поз.	Наименование и техническая характеристика	Тип, марка, обозначение документа	Код продукции	Поставщик	Ед. изм.	Кол.	Образец	Примечание
	Плитка и керамогранит							
15	SG501600R, 600×1200 мм, противоскольжение R10	SG501600R		Kerama Marazzi	м²	23,04		шов 2 мм; Санузел, пол; Ванная, пол; Прихожая, пол; Коридор, пол; по раскладке 28 шт (S = 15,34 м²), с запасом 32 шт
16	610010001195, 1200×600 мм	610010001195		Italon	м²	56,16		шов 2 мм; Санузел, стены А–Г; Ванная, стены А–Г; по раскладке 70 шт (S = 32,62 м²), с запасом 78 шт
	Напольные покрытия							
17	1167-1101, рабочий слой 4 мм, эмиссия E1, укладка на клей	1167-1101		Coswick	м²	21,8		пом. 1, 9; S = 20,35 м² (пол + половина стены в дверных проёмах, как в смете) + 7 %; к заказу — кратно упаковке
18	1167-1101, класс 33, рабочий слой 4 мм, эмиссия E1, укладка на клей	1167-1101		Coswick	м²	32		пом. 2, 3, 8; S = 29,86 м² (пол + половина стены в дверных проёмах, как в смете) + 7 %; к заказу — кратно упаковке
19	Клей для паркета и инженерной доски, эластичный (СМП / полиуретановый)	по рекомендации производителя доски			м²	51		площадь приклейки; расход и шпатель — по ТУ клея
	Погонажные изделия							
20	SX165, h = 69 мм, крепление к стене, окраска в цвет Tikkurila V503	SX165		Orac Decor	м	9		пом. 1; L = 7,8 м (периметр без дверных проёмов) + 10 % на подрезку; в штуках — по длине планки
21	SX165, h = 69 мм, крепление к стене, окраска в цвет NCS S 0300-N	SX165		Orac Decor	м	53		пом. 2, 3, 4, 5, 8; L = 47,4 м (периметр без дверных проёмов) + 10 % на подрезку; в штуках — по длине планки
22	SX165, h = 69 мм, крепление к стене, окраска в цвет Farrow & Ball No. 241	SX165		Orac Decor	м	18		пом. 9; L = 15,9 м (периметр без дверных проёмов) + 10 % на подрезку; в штуках — по длине планки
	Смеси и материалы для облицовки							
23	Затирка для швов плитки	аналог по характеристикам			кг	3,7		по раскладке (a+b)/(a·b) × шов × t × 1,6 + 10 %
24	Клей плиточный C2 S1 по EN 12004, слой 5 мм	аналог по характеристикам			кг	36		2 меш. по 25 кг; 1,5 кг/м² на 1 мм слоя + 10 %
25	Клей плиточный C2 по EN 12004, слой 5 мм	аналог по характеристикам			кг	271		11 меш. по 25 кг; 1,5 кг/м² на 1 мм слоя + 10 %
26	Гидроизоляция обмазочная мокрых зон: пол, стены по периметру, зоны замачивания; 2 слоя с армирующей лентой в углах	аналог по характеристикам			м²	8,9		площадь по листу раскладки плитки + 10 %; расход смеси — по ТУ
27	Лента демпферная по периметру пола из плитки	аналог по характеристикам			м	27		периметр без дверных проёмов + 10 %

Примечания

1. Количества — из геометрии проекта: площади поверхностей по чистым граням стен до отделки (те же, что в ведомости отделки и колерной карте), плитка, клей и затирка — по раскладке плиточника; в графе «Кол.» — к заказу, с запасом.
2. Краска: расход 0,12 л/м² на слой в 2 слоя, если по ТУ не задан иной; запас 10 % и 0,5 л на подкраску каждого кода. Один код — одна партия, колеровка машинная в колеровочном центре бренда; в заказ — только после утверждения выкраса (колерная карта). Фасовка — по каталогу бренда на дату выпуска; к заказу — не меньше расчётного объёма.
3. «Аналог по характеристикам» — допускается изделие другого производителя с характеристиками не ниже указанных, по согласованию с автором проекта.
4. Графы «Код продукции» и «Масса 1 ед.» не заполнены: коды по классификатору продукции не присвоены, масса единицы до 25 кг (ГОСТ 21.110-2013).
5. Грунтовка и клей для доски указаны площадью обработки; объём — по ТУ выбранного продукта.

	Лист	№ док.	Подпись	Дата	Проект: Квартира 65 м²			
Дизайнер	Кырлан А.С.			14.11.26	Спецификация отделочных материалов	Стадия	Лист	Листов
Проверил						П	С3	105
Н. контр.								
Утв.								

Список покупок: материалы для магазина

№	Что купить	Артикул или характеристика	Нужно с запасом	Брать в магазине	Фасовка	Уточнить в магазине	Помещения	Кто покупает
Покрытия полов и облицовка								
1	Инженерная доска (дуб натуральный, рабочий слой 4 мм, эмиссия E1, прямая укладка)	1167-1101	53,72 м²	53,8 м²		уточнить в магазине: м² в упаковке	1, 2, 3, 8, 9	по проекту
2	Клей для паркетной и инженерной доски (эластичный, по ТУ изготовителя доски)	на выбор бригады по проекту	50,21 м²			уточнить в магазине: расход и фасовку — по выбранному продукту		бригада
3	Керамогранит 600×1200 мм SG501600R	SG501600R	31 шт	32 шт		уточнить в магазине: штук в коробке	4, 5, 6, 7	по проекту
4	Керамогранит 1200×600 мм 610010001195	610010001195	77 шт	78 шт		уточнить в магазине: штук в коробке	6, 7	по проекту
Сухие смеси и гидроизоляция								
5	Клей плиточный цементный класса C2 S1 (ГОСТ Р 56387-2018)	на выбор бригады по проекту	35,38 кг	2 меш.	мешок 25 кг			по проекту
6	Клей плиточный цементный класса C2 (ГОСТ Р 56387-2018)	на выбор бригады по проекту	270,51 кг	11 меш.	мешок 25 кг			по проекту
7	Затирка цементная класса класс не задан, цвет — по колерной карте	на выбор бригады по проекту	3,67 кг	2 упак.	упак. 2 кг			по проекту
8	Гидроизоляция обмазочная полимерная, 2 слоя, лента в углах, манжеты на выводах	на выбор бригады по проекту	8,94 м²			уточнить в магазине: расход и фасовку — по выбранному продукту	6, 7	бригада
9	Лента демпферная по периметру пола из плитки	на выбор бригады по проекту	27,02 м	28 м		уточнить в магазине: фасовку		бригада
10	Смесь цементно-песчаная для стяжки М200 (50 мм, 33 мм)	на выбор бригады по проекту	3,37 м³			уточнить в магазине: расход и фасовку — по выбранному продукту		бригада
11	Смесь штукатурная гипсовая для машинного и ручного нанесения по маякам, слой до 10 мм	на выбор бригады по проекту	64,89 м²			уточнить в магазине: расход и фасовку — по выбранному продукту	1, 9	бригада
Перегородки и облицовки из ГКЛВ								
12	Лист ГКЛ 12,5 мм, 2500 × 1200 мм: обшивка перегородок и облицовок, 2 слоя на сторону	на выбор бригады по проекту	20,77 м²	7 лист.	лист 3,00 м²			бригада
13	Профиль направляющий ПН 100: по потолку и полу, перемычки над проёмами	на выбор бригады по проекту	3,85 м	2 шт	хлыст 3 м			бригада
14	Профиль стоечный ПС 100: стойки через шаг каркаса и короткие над проёмами	на выбор бригады по проекту	11,88 м	4 шт	хлыст 3 м			бригада
15	Плита минераловатная звукопоглощающая в полость каркаса, толщина по глубине профиля 100 мм	на выбор бригады по проекту	5,19 м²			уточнить в магазине: расход и фасовку — по выбранному продукту		бригада
16	Лента уплотнительная самоклеящаяся под профили по потолку, полу и у примыканий к стенам	на выбор бригады по проекту	3,85 м	4 м		уточнить в магазине: фасовку		бригада
17	Саморезы для ГКЛ по металлу (по слоям обшивки), дюбели для направляющих — по ТУ изготовителя системы	на выбор бригады по проекту	18,88 м²			уточнить в магазине: расход и фасовку — по выбранному продукту		бригада
Слаботочные сети								
18	Кабель домофона — тип по системе поставщика	на выбор бригады по проекту	3,1 м	4 м		уточнить в магазине: длину бухты		бригада
19	Кабель коаксиальный RG-6 (75 Ом) к розеткам ТВ	на выбор бригады по проекту	30,2 м	31 м		уточнить в магазине: длину бухты		бригада
20	Кабель U/UTP кат. 5e (LAN, Wi-Fi и камеры по PoE)	на выбор бригады по проекту	42,7 м	43 м		уточнить в магазине: длину бухты		бригада
21	Кабель U/UTP кат. 6 (LAN, Wi-Fi и камеры по PoE)	на выбор бригады по проекту	14,2 м	15 м		уточнить в магазине: длину бухты		бригада
22	Гофротруба Ø20 для слаботочных линий, отдельно от силовых	на выбор бригады по проекту	81,2 м	82 м		уточнить в магазине: длину бухты		бригада

	Лист	№ док.	Подпись	Дата	Проект: Квартира 65 м²			
Дизайнер	Кырлан А.С.			14.11.26				
Проверил					Список покупок	Стадия	Лист	Листов
Н. контр.						П	С4	105
Утв.								

Список покупок: материалы для магазина (продолжение)

№	Что купить	Артикул или характеристика	Нужно с запасом	Брать в магазине	Фасовка	Уточнить в магазине	Помещения	Кто покупает
23	Розетка компьютерная RJ45, кат. 6, с рамкой и подрозетником	на выбор бригады по проекту	4 шт	4 шт	шт			бригада
24	Розетка телевизионная (коаксиальная) с рамкой и подрозетником	на выбор бригады по проекту	2 шт	2 шт	шт			бригада
25	Трубка или монитор домофона (поставка домофонной организации)	на выбор бригады по проекту	1 шт	1 шт	шт			по проекту
26	Щит слаботочный ЩС: корпус, DIN-рейка, розетки 220 В	на выбор бригады по проекту	1 шт	1 шт	шт			бригада
27	Патч-панель, портов не менее 4	на выбор бригады по проекту	1 шт	1 шт	шт			бригада
Лакокрасочные материалы								
28	Краска интерьерная акриловая, матовая, класс истирания 1	Tikkurila Harmony V503 «Winter»	5,64 л	3 банк.	банка 2,7 л		1	по проекту
29	Краска интерьерная акриловая, глубокоматовая, класс истирания 2	Tikkurila Anti-Reflex 2 V503 «Winter»	5,34 л	2 банк.	банка 2,7 л		1, 9	по проекту
30	Краска интерьерная акриловая, глубокоматовая, класс истирания 2	Tikkurila S 1502-Y50R	6,63 л	3 банк.	банка 2,7 л		2	по проекту
31	Краска интерьерная водно-дисперсионная, глубокоматовая, класс истирания 2	Tikkurila S 0300-N	11,88 л	5 банк.	банка 2,7 л		2, 3, 4, 5, 6, 7, 8	по проекту
32	Краска интерьерная акриловая, полуматовая, класс истирания 1	Tikkurila S 1002-Y50R	12,22 л	5 банк.	банка 2,7 л		3	по проекту
33	Краска интерьерная акриловая, полуматовая, класс истирания 1	Tikkurila S 1502-Y50R	9,82 л	4 банк.	банка 2,7 л		4, 5	по проекту
34	Краска интерьерная акриловая, матовая, класс истирания 2	Tikkurila S 0502-Y	4,14 л	2 банк.	банка 2,7 л		8	по проекту
35	Краска интерьерная акриловая, матовая, класс истирания 1	Farrow & Ball Modern Emulsion No. 30 «Hague Blue»	3,52 л	2 банк.	банка 2,5 л		9	по проекту
36	Краска интерьерная акриловая, матовая, класс истирания 1	Farrow & Ball Modern Emulsion No. 241 «Skimming Stone»	6,4 л	3 банк.	банка 2,5 л		9	по проекту
37	Шпаклёвка финишная полимерная под окраску (стены и потолки, Q3)	на выбор бригады по проекту	273,36 м²			уточнить в магазине: расход и фасовку — по выбранному продукту		бригада
38	Грунтовка акриловая глубокого проникновения, 2 слоя	на выбор бригады по проекту	309,24 м²			уточнить в магазине: расход и фасовку — по выбранному продукту		бригада
Погонажные изделия и потолки								
39	Плинтус напольный МДФ под покраску, h=69 мм, крепление к стене	SX165	78,16 м.п.	33 шт	хлыст 2,4 м		1, 2, 3, 4, 5, 8, 9	по проекту
40	Потолок подвесной ГКЛ/ГКЛВ по каркасу Knauf П113: листы, профили, подвесы, лента, шпаклёвка швов	Knauf П113	58,54 м²		комплект	уточнить в магазине: расход и фасовку — по выбранному продукту		по проекту

Примечания

1. «Нужно с запасом» — расход по чертежам и раскладке плюс запас на подрезку и подкраску; «Брать в магазине» — то же количество в единицах, которыми продают (банки, мешки, упаковки, листы, штуки, литры).
2. «Уточнить в магазине» — фасовки этого товара в проекте нет: спросите у продавца, сколько в упаковке, и возьмите целое число упаковок не меньше «Нужно с запасом».
3. Плитку, доску и краску одного цвета берите одной партией (один калибр и тон на помещение) и сохраните чек и номер партии до конца ремонта.
4. «По характеристике» — артикул не выбран: подойдёт любой товар с этими свойствами, согласуйте его с дизайнером до покупки. «Бригада» материал выбирает и закупает бригада по своей технологии.
5. Помещения: 1 — Гардеробная; 2 — Спальня; 3 — Кухня-гостиная; 4 — Прихожая; 5 — Коридор; 6 — Санузел; 7 — Ванная; 8 — Кладовая; 9 — Детская; «—» — материал для нескольких помещений, расход по месту.

	Лист	№ док.	Подпись	Дата	Проект: Квартира 65 м²			
Дизайнер	Кырлан А.С.			14.11.26	Список покупок (окончание)	Стадия	Лист	Листов
Проверил						П	С5	105
Н. контр.								
Утв.								

Смета проекта: весь проект по категориям (прайсы собраны 21.09.2026, часть расценок сверена повторно 06.10.2026 и 08.11.2026)

Категория	Позиций	С ценой	По КП	Сумма по позициям с ценой, ₽
Ремонт: работы	51	32	19	861 714
Ремонт: материалы отделки и черновые	35	15	20	668 783
Электрика: кабель, механизмы, щит	34	0	34	
Сантехника: приборы, трубы, арматура	33	0	33	
Доставка и услуги	4	1	3	66 878
Мебель (включая кухню)	21	0	21	
Свет: светильники и ленты	27	0	27	
Техника	3	0	3	
Декор и текстиль	44	0	44	
ИТОГО по позициям с ценой (цены — нижняя граница открытых прайсов)	**252**	**48**	**204**	**1 597 375**
Резерв на непредвиденные работы и материалы, 15 % от ремонта				239 606
ВЕСЬ ПРОЕКТ — вилка «от … до …», ₽				**1 597 375 … 1 836 981**
Позиции «по КП» — цена не названа, в итог НЕ входят: работы — 19; материалы отделки и черновые — 20; электрика: кабель, механизмы, щит — 34; сантехника: приборы, трубы, арматура — 33; доставка и услуги — 3; мебель (включая кухню) — 21; свет: светильники и ленты — 27; техника — 3; декор и текстиль — 44			**204**	**итог выше на их цену**

По этапам

Этап	Поз.	С ценой	Сумма, ₽
Демонтаж и черновые работы (работы)	12	6	167 012
Инженерные системы (работы)	22	11	104 987
Чистовые работы (работы)	17	15	589 715
Черновые материалы (смеси, ГКЛ, гидроизоляция)	17	2	23 400
Электрика: кабель, механизмы, щит, слаботочка	34	0	
Сантехника: приборы, трубы, арматура	33	0	
Чистовые материалы (отделка, двери)	18	13	645 383
Доставка и услуги	4	1	66 878
Резерв на непредвиденное, 15 %	1	1	239 606
Итого ремонт (с резервом)			**1 836 981**

По помещениям

Помещение	Работы, ₽	Материалы, ₽	Всего, ₽
Общее по объекту (без привязки к помещению)	20 208		20 208
1. Гардеробная	61 767	33 829	95 596
2. Спальня	95 361	55 908	151 269
3. Кухня-гостиная	188 453	119 979	308 432
4. Прихожая	50 372	17 903	68 275
5. Коридор	86 657	23 072	109 729
6. Санузел	62 055	111 403	173 458
7. Ванная	90 936	170 456	261 392
8. Кладовая	31 714	21 251	52 965
9. Детская	174 191	114 982	289 173
Доставка и услуги			66 878
Резерв 15 %			239 606
Итого ремонт (с резервом)			**1 836 981**

	Лист	№ док.	Подпись	Дата	Проект: Квартира 65 м²			
Дизайнер	Кырлан А.С.			14.11.26	Смета проекта: этапы, помещения, итог	Стадия	Лист	Листов
Проверил						П	С6	105
Н. контр.								
Утв.								

Работы по этапам с расценками (ориентир)

№	Работа	Ед.	Объём	Расценка, ₽	Сумма, ₽	Расценка	Чей подряд
1. Демонтаж и черновые работы — работы, ориентир по открытым прайсам							
1	Демонтаж существующего покрытия пола до основания	м²	65,24	по КП			бригада
2	Демонтаж существующей отделки стен до основания	м²	215,89	по КП			бригада
3	Демонтаж существующей отделки потолка до основания	м²	65,24	по КП			бригада
4	Демонтаж существующих дверных блоков	шт	8,00	по КП			бригада
5	Демонтаж существующих сантехприборов и электрооборудования (если есть)	компл		по КП			бригада
6	Монтаж каркасной перегородки П-1: каркас ПС через 600 мм, ГКЛ в 2 слоя с каждой стороны	м²	4,72	1 500	7 080	Ц1	бригада
7	Заполнение каркаса П-1 минераловатной плитой (звукоизоляция, Rw — дБ)	м²	4,72	по КП			бригада
8	Устройство стяжки: стяжка ЦПС М200, 50 мм	м²	66,11	530	35 038	Ц1	бригада
9	Гидроизоляция обмазочная, 2 слоя: пол, стены на 200 мм, зоны замачивания	м²	8,13	450	3 659	Ц1	бригада
10	Штукатурка стен по маякам, до 10 мм	м²	58,99	530	31 265	Ц1	бригада
11	Штукатурка оконных откосов шириной более 200 мм	м²	4,00	540	2 160	Ц4	бригада
12	Потолок ГКЛ по каркасу П113, 1 слой	м²	58,54	1 500	87 810	Ц1	бригада
2. Инженерные системы — работы, ориентир по открытым прайсам							
13	Прокладка слаботочной линии: Кабель домофона — тип по системе поставщика, отдельно от силовых	м	3,10	по КП			бригада
14	Прокладка слаботочной линии: Кабель коаксиальный RG-6 (75 Ом) к розеткам ТВ, отдельно от силовых	м	30,20	по КП			бригада
15	Прокладка слаботочной линии: Кабель U/UTP кат. 5e (LAN, Wi-Fi и камеры по PoE), отдельно от силовых	м	42,70	по КП			бригада
16	Прокладка слаботочной линии: Кабель U/UTP кат. 6 (LAN, Wi-Fi и камеры по PoE), отдельно от силовых	м	14,20	по КП			бригада
17	Прокладка гофротрубы Ø20 для слаботочных линий, отдельно от силовых	м	81,20	140	11 368	Ц3	бригада
18	Сборка слаботочного щита ЩС: корпус, патч-панель, подключение линий и питания 220 В; коммутатор и точки доступа — оборудование заказчика	шт	1,00	по КП			бригада
19	Электроточка: подрозетник в бетоне, розетка, выключатель, вывод	шт	39,00	950	37 050	Ц3	бригада
20	Штробы в стенах под спуски кабеля к точкам — выполняются только после технического заключения о несущих стенах	м	69,81	по КП			бригада
21	Установка встраиваемого точечного светильника	шт	11,00	750	8 250	Ц3	бригада
22	Монтаж светильника: потолочного, подвесного, настенного	шт	13,00	1 200	15 600	Ц3	бригада
23	Монтаж LED-ленты в алюминиевый профиль	м	16,30	230	3 749	Ц3	бригада
24	Установка блока питания LED в доступном месте (люк, шкаф)	шт	3,00	570	1 710	Ц3	бригада
25	Установка автономного пожарного извещателя	шт	5,00	по КП			бригада
26	Сборка щита: установка автоматов и АВДТ групп, вводного автомата	шт	6,00	230	1 380	Ц3	бригада
27	Установка вводного УЗО	шт	1,00	380	380	Ц3	бригада
28	Монтаж инсталляции, установка подвесного унитаза и кнопки смыва	шт	1,00	10 500	10 500	Ц1	бригада
29	Короб инсталляции: каркас и обшивка ГКЛВ в 2 слоя, ревизионный доступ к смыву	шт	2,00	по КП			бригада
30	Короб К1 над чистым полом: каркас и обшивка ГКЛВ под плитку (материалы — в спецификации ВК)	м	2,61	по КП			бригада
31	Установка ванны с сифоном	шт	1,00	6 000	6 000	Ц1	бригада

	Лист	№ док.	Подпись	Дата	Проект: Квартира 65 м²			
Дизайнер	Кырлан А.С.			14.11.26	Смета проекта: этапы, помещения, итог (продолжение)	Стадия	Лист	Листов
Проверил						П	С7	105
Н. контр.								
Утв.								

выпуск 14.11.2026 № 3aed0ef730 · стр. 94 из 105

Работы по этапам с расценками (ориентир) (продолжение)

№	Работа	Ед.	Объём	Расценка, ₽	Сумма, ₽	Расценка	Чей подряд
32	Установка умывальника (мойки) с сифоном и смесителем	шт	3,00	3 000	9 000	Ц1	бригада
33	Подключение стиральной (посудомоечной) машины к ВК	шт	1,00	по КП			бригада
34	Установка радиатора с узлом подключения и терморегулятором	шт	4,00	по КП			бригада
3. Чистовые работы — работы, ориентир по открытым прайсам							
35	Облицовка стен керамогранитом 1200×600 на клею	м²	32,62	2 500	81 550	Ц5	бригада
36	Укладка керамогранита на пол, 600×1200, на клею	м²	15,91	1 800	28 638	Ц2	бригада
37	Затирка швов керамогранита	м²	47,96	150	7 194	Ц2	бригада
38	Грунтование стен, 2 слоя (под штукатурку и под отделку)	м²	215,89	96	20 725	Ц4	бригада
39	Шпаклёвка стен под окраску, 2 слоя (старт и финиш), уровень Q3	м²	183,27	750	137 453	Ц1	бригада
40	Грунтование и шпаклёвка оконных откосов, 2 слоя	м	17,40	300	5 220	Ц4	бригада
41	Грунтование потолка, 2 слоя	м²	65,24	96	6 263	Ц4	бригада
42	Шпаклёвка потолка под окраску, 2 слоя, уровень Q3	м²	65,24	950	61 978	Ц1	бригада
43	Окраска потолка водно-дисперсионной краской, 2 слоя	м²	65,24	360	23 486	Ц1	бригада
44	Окраска стен водно-дисперсионной краской, 2 слоя	м²	216,14	300	64 842	Ц1	бригада
45	Окраска оконных откосов, 2 слоя	м	17,40	120	2 088	Ц4	бригада
46	Укладка инженерной доски на клей	м²	50,20	1 200	60 240	Ц1	бригада
47	Установка плинтуса МДФ h=69 мм	м	71,05	450	31 973	Ц1	бригада
48	Окраска плинтуса в тоне V503, 2 слоя	м	71,05	300	21 315	Ц1	бригада
49	Монтаж дверей скрытого монтажа под покраску (поставщик дверей)	шт	7,00	5 250	36 750	Ц1	поставщик
50	Входная дверь, поставка с монтажом и откосами	шт	1,00	по КП			поставщик
51	Монтаж телевизора ОБ-01 на кронштейн, скрытая прокладка HDMI и питания (штроба, трубка), подключение акустики	шт	1,00	по КП			бригада
4. Прочие работы и услуги — работы, ориентир по открытым прайсам							
52	Кухонный гарнитур по проекту кухни, изготовление и монтаж (4–8 нед.)	компл	1,00	по КП			поставщик
	Итого работы (позиции с расценкой)				**861 714**		

Примечания

1. Итог «ВЕСЬ ПРОЕКТ» — не прогноз, а сумма того, у чего есть цена: ремонт (работы и материалы по смете сметчика), мебель, свет, техника и декор — по ценам из данных проекта. Позиции без цены названы «по КП» (204 шт.) и в итог не входят: пока цена не названа, итог выше напечатанного.
2. Вилка: «от» — сумма по позициям с ценой по нижней границе открытых прайсов (прайсы собраны 21.09.2026, часть расценок сверена повторно 06.10.2026 и 08.11.2026, Москва); «до» — «от» плюс резерв на непредвиденное (15 % от ремонта; частный ремонт 10–20 %).
3. Работы — ориентир по прайсам подрядчиков, не договорная цена: расценку называет бригада после контрольного обмера. Материалы — по «Смете материалов с ценами» (следующий лист).
4. Разбивка по помещениям — доли: общая закупка делится пропорционально площади (длине, числу), по которой считается позиция; работы — по объёму строки в помещении. Сумма по помещениям, по этапам и по категориям одна и та же.
5. Источники расценок и цен: Ц1 — Домашний мастерок: прайс на отделочные работы, 2026; Ц2 — Домашний мастерок: прайс на плиточные работы, 2026; Ц3 — Домашний мастерок: прайс на электромонтажные работы, 2026; Ц4 — Профи ремонтник: штукатурно-малярные работы; Ц5 — Profi.ru: укладка керамогранита на стены, Москва 2026; Ц6 — справочник материалов: ориентир по сегментам; Ц7 — Розница Москвы, 09.2026: Лемана ПРО, KGSnab, официальный дилер Farrow & Ball.
6. Оборудование «по КП» из сметы сметчика (кухня и др.): 1 поз. — в позиции «по КП» мебели и техники.

	Лист	№ док.	Подпись	Дата	Проект: Квартира 65 м²			
Дизайнер	Кырлан А.С.			14.11.26				
Проверил					Смета проекта: этапы, помещения, итог (окончание)	Стадия	Лист	Листов
Н. контр.								
Утв.						П	С8	105

Смета материалов с ценами

№	Позиция	Ед.	Нетто	Запас	С запасом	К закупке (упаковка)	Цена за ед., ₽	Сумма, ₽	Заказать заранее	Доп.
Чистовая отделка — позиций 18, с ценой 13, итого 645 383 ₽										
Покрытия полов и облицовка										
1	Инженерная доска (дуб натуральный, рабочий слой 4 мм, эмиссия E1, прямая укладка) — 1167-1101	м²	50,21	7 %	53,72	53,80 м²	4 513 / м²	242 799		8
2	Керамогранит 600×1200 мм SG501600R	шт	28	14 %	32	32 шт · коробка	3 500 / м²	80 640		8
3	Керамогранит 1200×600 мм 610010001195	шт	70	11 %	78	78 шт · коробка	3 500 / м²	196 560		8
Лакокрасочные материалы										
4	Краска интерьерная акриловая, матовая, класс истирания 1 — Tikkurila Harmony V503 «Winter»	л	5,13	10 %	5,64	3 банка · банка 2,7 л	3 510 / банк	10 530		8
5	Краска интерьерная акриловая, глубокоматовая, класс истирания 2 — Tikkurila Anti-Reflex 2 V503 «Winter»	л	4,85	10 %	5,33	2 банка · банка 2,7 л	3 510 / банк	7 020		8
6	Краска интерьерная акриловая, глубокоматовая, класс истирания 2 — Tikkurila S 1502-Y50R	л	6,03	10 %	6,63	3 банка · банка 2,7 л	3 510 / банк	10 530		8
7	Краска интерьерная водно-дисперсионная, глубокоматовая, класс истирания 2 — Tikkurila S 0300-N	л	10,80	10 %	11,88	5 банка · банка 2,7 л	3 510 / банк	17 550		8
8	Краска интерьерная акриловая, полуматовая, класс истирания 1 — Tikkurila S 1002-Y50R	л	11,11	10 %	12,22	5 банка · банка 2,7 л	3 510 / банк	17 550		8
9	Краска интерьерная акриловая, полуматовая, класс истирания 1 — Tikkurila S 1502-Y50R	л	8,93	10 %	9,82	4 банка · банка 2,7 л	3 510 / банк	14 040		8
10	Краска интерьерная акриловая, матовая, класс истирания 2 — Tikkurila S 0502-Y	л	3,76	10 %	4,14	2 банка · банка 2,7 л	3 510 / банк	7 020		8
11	Краска интерьерная акриловая, матовая, класс истирания 1 — Farrow & Ball Modern Emulsion No. 30 «Hague Blue»	л	3,20	10 %	3,52	2 банка · банка 2,5 л	5 800 / банк	11 600		8
12	Краска интерьерная акриловая, матовая, класс истирания 1 — Farrow & Ball Modern Emulsion No. 241 «Skimming Stone»	л	5,82	10 %	6,40	3 банка · банка 2,5 л	5 800 / банк	17 400		8
Погонажные изделия и потолки										
13	Плинтус напольный МДФ под покраску, h=69 мм, крепление к стене — SX165	м	71,05	10 %	78,16	33 шт · хлыст 2,4 м	368 / шт	12 144		8
Двери										
14	Дверь входная Д-1, проём 900×2100 мм	шт	1		1	1 шт	по запросу			6
15	Дверь скрытого монтажа (короб под покраску) Д-2, проём 800×2100 мм, Profil Doors Invisible Скрытая дверь Invisible	шт	2		2	2 шт	по запросу		≈ 30 дн.	6, 7
16	Дверь скрытого монтажа (короб под покраску) Д-3, проём 700×2100 мм, Profil Doors Invisible Скрытая дверь Invisible	шт	3		3	3 шт	по запросу		≈ 30 дн.	6, 7
17	Дверь скрытого монтажа (короб под покраску) Д-4, проём 700×2100 мм, Profil Doors Invisible Скрытая дверь Invisible	шт	1		1	1 шт	по запросу		≈ 30 дн.	6, 7
18	Дверь скрытого монтажа (короб под покраску) Д-5, проём 550×2100 мм, Profil Doors Invisible Скрытая дверь Invisible	шт	1		1	1 шт	по запросу		≈ 30 дн.	6, 7
Черновые материалы — позиций 17, с ценой 2, итого 23 400 ₽										
Покрытия полов и облицовка										
19	Клей для паркетной и инженерной доски (эластичный, по ТУ изготовителя доски)	м²	50,21		50,21	фасовка по ТУ изделия	по запросу			2
Сухие смеси и гидроизоляция										
20	Клей плиточный цементный класса C2 S1 (ГОСТ Р 56387-2018)	кг	32,16	10 %	35,38	2 мешок · мешок 25 кг	1 800 / меш.	3 600		8
21	Клей плиточный цементный класса C2 (ГОСТ Р 56387-2018)	кг	245,92	10 %	270,51	11 мешок · мешок 25 кг	1 800 / меш.	19 800		8
22	Затирка цементная класса класс не задан, цвет — по колерной карте	кг	3,34	10 %	3,67	2 упаковка · упак. 2 кг	по запросу			
23	Гидроизоляция обмазочная полимерная, 2 слоя, лента в углах, манжеты на выводах	м²	8,13	10 %	8,94	фасовка по ТУ изделия	по запросу			2
24	Лента демпферная по периметру пола из плитки	м	24,56	10 %	27,02	28,00 м	по запросу			
25	Смесь цементно-песчаная для стяжки М200 (50 мм, 33 мм)	м³	3,21	5 %	3,37	фасовка по ТУ изделия	по запросу			2
26	Смесь штукатурная гипсовая для машинного и ручного нанесения по маякам, слой до 10 мм	м²	58,99	10 %	64,89	фасовка по ТУ изделия	по запросу			2

	Лист	№ док.	Подпись	Дата
Дизайнер	Кырлан А.С.			14.11.26
Проверил				
Н. контр.				
Утв.				

Проект: Квартира 65 м²

Смета материалов с ценами	Стадия	Лист	Листов
	П	С9	105

Смета материалов с ценами (продолжение)

№	Позиция	Ед.	Нетто	Запас	С запасом	К закупке (упаковка)	Цена за ед., ₽	Сумма, ₽	Заказать заранее	Доп.
Перегородки и облицовки из ГКЛВ										
27	Лист ГКЛ 12,5 мм, 2500 × 1200 мм: обшивка перегородок и облицовок, 2 слоя на сторону	м²	18,88	10 %	20,77	7 лист · лист 3,00 м²	по запросу			
28	Профиль направляющий ПН 100: по потолку и полу, перемычки над проёмами	м	3,50	10 %	3,85	2 шт · хлыст 3 м	по запросу			
29	Профиль стоечный ПС 100: стойки через шаг каркаса и короткие над проёмами	м	10,80	10 %	11,88	4 шт · хлыст 3 м	по запросу			
30	Плита минераловатная звукопоглощающая в полость каркаса, толщина по глубине профиля 100 мм	м²	4,72	10 %	5,19	фасовка по ТУ изделия	по запросу			2
31	Лента уплотнительная самоклеящаяся под профили по потолку, полу и у примыканий к стенам	м	3,50	10 %	3,85	4,00 м	по запросу			
32	Саморезы для ГКЛ по металлу (по слоям обшивки), дюбели для направляющих — по ТУ изготовителя системы	м²	18,88		18,88	фасовка по ТУ изделия	по запросу			2
Лакокрасочные материалы										
33	Шпаклёвка финишная полимерная под окраску (стены и потолки, Q3)	м²	248,51	10 %	273,36	фасовка по ТУ изделия	по запросу			2
34	Грунтовка акриловая глубокого проникновения, 2 слоя	м²	281,13	10 %	309,24	фасовка по ТУ изделия	по запросу			2
Погонажные изделия и потолки										
35	Потолок подвесной ГКЛ/ГКЛВ по каркасу Knauf П113: листы, профили, подвесы, лента, шпаклёвка швов	м²	58,54		58,54	фасовка по ТУ изделия	по запросу			2
Электрика и слаботочные сети — позиций 34, с ценой 0, итого 0 ₽										
Слаботочные сети										
36	Кабель домофона — тип по системе поставщика	м	3,10		3,10	4,00 м	по запросу			3
37	Кабель коаксиальный RG-6 (75 Ом) к розеткам ТВ	м	30,20		30,20	31,00 м	по запросу			3
38	Кабель U/UTP кат. 5e (LAN, Wi-Fi и камеры по PoE)	м	42,70		42,70	43,00 м	по запросу			3
39	Кабель U/UTP кат. 6 (LAN, Wi-Fi и камеры по PoE)	м	14,20		14,20	15,00 м	по запросу			3
40	Гофротруба Ø20 для слаботочных линий, отдельно от силовых	м	81,20		81,20	82,00 м	по запросу			3
41	Розетка компьютерная RJ45, кат. 6, с рамкой и подрозетником	шт	4		4	4 шт	по запросу			
42	Розетка телевизионная (коаксиальная) с рамкой и подрозетником	шт	2		2	2 шт	по запросу			
43	Трубка или монитор домофона (поставка домофонной организации)	шт	1		1	1 шт	по запросу			
44	Щит слаботочный ЩС: корпус, DIN-рейка, розетки 220 В	шт	1		1	1 шт	по запросу			
45	Патч-панель, портов не менее 4	шт	1		1	1 шт	по запросу			
Электрика: щит										
46	Автоматический выключатель C10 A, 1P	шт	1		1	1 шт	по запросу			4
47	Автоматический выключатель C16 A, 1P	шт	3		3	3 шт	по запросу			4
48	Автоматический выключатель C32 A, 1P	шт	1		1	1 шт	по запросу			4
49	Корпус щита ЩРВ-П-24, IP41, 24 модулей	шт	1		1	1 шт	по запросу			4
50	Вводной автомат C63, 2P	шт	1		1	1 шт	по запросу			4
51	Вводное УЗО-S 63 A, 100 мА (селективное)	шт	1		1	1 шт	по запросу			4
52	УЗИП тип 2	шт	1		1	1 шт	по запросу			4
Электрика: механизмы и изделия										
53	Розетка с з/к и защитными шторками, 16 A	шт	22		22	22 шт	по запросу			4

	Лист	№ док.	Подпись	Дата	Проект: Квартира 65 м²			
Дизайнер	Кырлан А.С.			14.11.26	Смета материалов с ценами (продолжение)	Стадия	Лист	Листов
Проверил						П	С10	105
Н. контр.								
Утв.								

Смета материалов с ценами (продолжение)

№	Позиция	Ед.	Нетто	Запас	С запасом	К закупке (упаковка)	Цена за ед., ₽	Сумма, ₽	Заказать заранее	Доп.
54	Розетка IP44 с крышкой, 16 А	шт	2		2	2 шт	по запросу			4
55	Выключатель 1-клав.	шт	1		1	1 шт	по запросу			4
56	Выключатель 1-клав. проходной	шт	3		3	3 шт	по запросу			4
57	Выключатель 2-клав.	шт	1		1	1 шт	по запросу			4
58	Выключатель 2-клав. (перекрёстная + проходная)	шт	1		1	1 шт	по запросу			4
59	Выключатель 2-клав. проходной	шт	2		2	2 шт	по запросу			4
60	Рамка 1-постовая	шт	26		26	26 шт	по запросу			4
61	Рамка 2-постовая	шт	3		3	3 шт	по запросу			4
62	Коробка установочная (подрозетник) Ø68	шт	32		32	32 шт	по запросу			4
63	Вывод кабеля под прибор (клеммник)	шт	3		3	3 шт	по запросу			4
64	Вывод кабеля к вентилятору вытяжки	шт	1		1	1 шт	по запросу			4
65	Коробка уравнивания потенциалов КУП	шт	1		1	1 шт	по запросу			4
66	Блок питания LED 24 В, 60 Вт	шт	2		2	2 шт	по запросу			4
67	Блок питания LED 24 В, 200 Вт, дим.	шт	1		1	1 шт	по запросу			4
68	Извещатель дымовой автономный	шт	3		3	3 шт	по запросу			4
69	Извещатель тепловой	шт	2		2	2 шт	по запросу			4
Сантехника — позиций 33, с ценой 0, итого 0 ₽										
Сантехника: санитарные приборы										
70	Ванна встраиваемая акриловая 1650×700 мм, с каркасом, экраном и отверстием слив-перелив — Ravak Classic C541000000	шт	1		1	1 шт	по запросу			5
71	Унитаз подвесной безободковый, с сиденьем микролифт, крепёж и звукоизолирующая прокладка — Jacob Delafon Struktura EDF102-00	шт	1		1	1 шт	по запросу			5
72	Инсталляция для подвесного унитаза: рама высотой 1120 мм, бачок, клавиша смыва (ось клавиши 1050 мм от чистого пола)	шт	1		1	1 шт	по запросу			5, 1
73	Умывальник подвесной 400×300 мм, с отверстием под смеситель и переливом — Roca The Gap 7.3274.7.400.0	шт	1		1	1 шт	по запросу			5
74	Умывальник подвесной 550×450 мм, с отверстием под смеситель и переливом — Roca The Gap 7.3274.7.400.0	шт	1		1	1 шт	по запросу			5
75	Мойка кухонная 700×480 мм, с переливом — мойка врезная 700×480 в шкафу М-11	шт	1		1	1 шт	по запросу			5
76	Полотенцесушитель электрический, IP44, с терморегулятором	шт	1		1	1 шт	по запросу			5, 1
Сантехника: смесители, сифоны и арматура приборов										
77	Смеситель для ванны настенный однорычажный, межосевое 150 мм, с душевым набором (лейка, шланг, держатель)	шт	1		1	1 шт	по запросу			5, 1
78	Смеситель для умывальника однорычажный, с донным клапаном	шт	2		2	2 шт	по запросу			5, 1
79	Смеситель кухонный однорычажный, высокий излив	шт	1		1	1 шт	по запросу			5, 1
80	Обвязка ванны слив-перелив Ø40/50 с сифоном	шт	1		1	1 шт	по запросу			5, 1
81	Сифон для умывальника бутылочный Ø32/40–50, с гофрой к выпуску	шт	2		2	2 шт	по запросу			5, 1
82	Сифон для мойки Ø40/50	шт	1		1	1 шт	по запросу			5, 1
83	Сифон для стиральной машины встраиваемый в стену Ø50, с обратным клапаном	шт	1		1	1 шт	по запросу			5, 1
84	Кран угловой ½"×½" с гибкой подводкой 40 см (умывальники, мойка)	шт	6		6	6 шт	по запросу			5, 1

	Лист	№ док.	Подпись	Дата	Проект: Квартира 65 м²			
Дизайнер	Кырлан А.С.			14.11.26	Смета материалов с ценами (продолжение)	Стадия	Лист	Листов
Проверил						П	С11	105
Н. контр.								
Утв.								

Смета материалов с ценами (продолжение)

№	Позиция	Ед.	Нетто	Запас	С запасом	К закупке (упаковка)	Цена за ед., ₽	Сумма, ₽	Заказать заранее	Доп.
85	Кран шаровой угловой ½"×¾" для подключения стиральной и посудомоечной машины	шт	1		1	1 шт	по запросу			5, 1
Сантехника: трубопроводы										
86	Труба полипропиленовая PP-R PN20 Ø20×3,4 (B1) — ГОСТ 32415-2013	м	17,00	10 %	17,00	17,00 м	по запросу			5
87	Труба PP-R, армированная стекловолокном, PN20 Ø20×2,8 (T3) — ГОСТ 32415-2013	м	12,00	10 %	12,00	12,00 м	по запросу			5
88	Труба канализационная ПП Ø50 (К1) — ГОСТ 32414-2013	м	13,00	10 %	13,00	13,00 м	по запросу			5
89	Труба канализационная ПП Ø110 (К1) — ГОСТ 32414-2013	м	1,50	10 %	1,50	1,50 м	по запросу			5
Сантехника: фасонные части и выводы										
90	Отвод канализационный ПП 45° Ø50 — ГОСТ 32414-2013	шт	20		20	20 шт	по запросу			5
91	Отвод канализационный ПП 45° Ø110 — ГОСТ 32414-2013	шт	6		6	6 шт	по запросу			5
92	Тройник канализационный ПП 45° (врезки ветвей) — ГОСТ 32414-2013	шт	5		5	5 шт	по запросу			5
93	Ревизия канализационная ПП (после поворота трассы) — ГОСТ 32414-2013	шт	8		8	8 шт	по запросу			5
94	Фитинги PP-R Ø20: тройники, угольники 90° (ветви и повороты B1, T3) — ГОСТ 32415-2013	шт	29		29	29 шт	по запросу			5
95	Водорозетка PP-R Ø20×½" настенная, с креплением — ГОСТ 32415-2013	шт	10		10	10 шт	по запросу			5
Сантехника: узлы ввода, люки, короба										
96	Кран шаровой латунный Ду15 PN16 (отключение ввода)	шт	2		2	2 шт	по запросу			5, 1
97	Фильтр сетчатый косой Ду15	шт	2		2	2 шт	по запросу			5, 1
98	Счётчик воды крыльчатый Ду15 (ХВ, ГВ), с поверкой	шт	2		2	2 шт	по запросу			5, 1
99	Клапан обратный Ду15	шт	2		2	2 шт	по запросу			5, 1
100	Люк ревизионный нажимной под плитку 300×400 мм	шт	3		3	3 шт	по запросу			5, 1
101	Звукоизоляция стояка К1 в коробе: рулонный звукоизоляционный материал ≥ 10 мм, обмотка стояка на высоту этажа	м	2,70		2,70	2,70 м	по запросу			5, 1
102	Короб К1 над полом: профиль ПН/ПС, ГКЛВ 12,5 мм под плитку	м	2,90		2,90	2,90 м	по запросу			5, 1
	ИТОГО материалы (позиций с ценой 15 из 102; без цены 87 — «по запросу», в итог не входят)							**668 783**		


Примечания

1. Количества — из единой книги материалов проекта: тот же расход, что в спецификации отделочных материалов, смете и списке покупок. Запас — на подрезку и бой; норма запаса печатается в графе «Запас», её основание — в отдельном документе «Смета на материалы».
2. Цены — нижняя граница открытых прайсов (прайсы собраны 21.09.2026, часть расценок сверена повторно 06.10.2026 и 08.11.2026, Москва); не предложение (оферта) магазинов. Цены нет — «по запросу», позиция в итог не входит. Работы в эту смету не входят (они — на листе «Смета проекта»).
3. Доп. 1. Изделие не выбрано: позиция описана по характеристикам («аналог»); марка, артикул и цена определяются при выборе изделия.
4. Доп. 2. Фасовка не задана в данных: количество дано в мерах расчёта, число упаковок определяется по выбранному продукту (расход и тара — по ТУ).
5. Доп. 3. Длина кабеля — по длинам групп щита из данных электрика; запас на подрезку в длину не заложен — берите бухту с запасом 5–10 %.
6. Доп. 4. Механизмы, рамки и подрозетники — по ведомости изделий электрика; серию механизмов выбирает заказчик.
7. Доп. 5. Трубы и фасонные части — по трассам листа разводки, +10 % на подрезку (уже в количестве); модели приборов заказчик выбирает сам.
8. Доп. 6. Двери: цена и срок называет поставщик после выбора изделия; в смету стоят только если цена задана в данных.
9. Доп. 7. Срок поставки — из данных проекта; если срок не задан, указан типовой диапазон практики как ориентир, а не срок поставщика.
10. Доп. 8. Цена — нижняя граница открытых прайс-листов на дату сбора (книга цен проекта); не коммерческое предложение магазина.
11. Доп. 9. Доли по помещениям справочные: общая закупка делится пропорционально площади (длине, числу), по которой считается позиция.

	Лист	№ док.	Подпись	Дата	Проект: Квартира 65 м²			
Дизайнер	Кырлан А.С.			14.11.26	Смета материалов с ценами (окончание)	Стадия	Лист	Листов
Проверил						П	С12	105
Н. контр.								
Утв.								

1 Порог 15 мм: мокрая зона — смежное помещение (М 1:5)


Применение: двери Д-5, Д-4

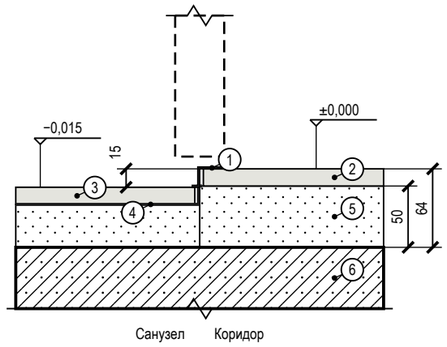

Поз.	Состав слоя, изделие
1	порог-переход металлический, перепад 15 мм, на клей-герметик
2	керамогранит на клею С2 TE S1
3	керамогранит на клею С2 TE S1
4	гидроизоляция в 2 слоя с подъёмом на торец ступени, лента в углу
5	ЦПС М200 50 мм; в мокрой зоне 33 мм
6	плита перекрытия

2 Дверь скрытого монтажа в плоскости стены, плинтус (М 1:5)


Применение: двери Д-3, Д-2, Д-5, Д-4

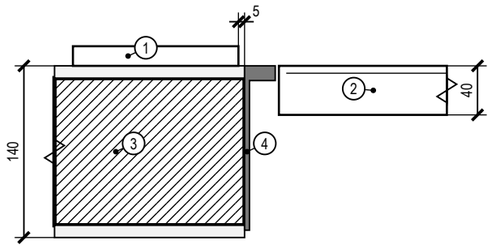

Поз.	Состав слоя, изделие
1	плинтус МДФ 69×16 на клей; у короба — зазор 5 мм, окраска в цвет стены
2	полотно 40 мм под окраску, заподлицо со стеной; теневой шов 3 мм
3	стена 120 мм, штукатурка 10 мм с двух сторон
4	короб скрытого монтажа (алюминий), лицом в плоскости отделки; монтаж до штукатурки

3 Короб стояков К1-1 с люком и звукоизоляцией (М 1:20)


Применение: пом. 6

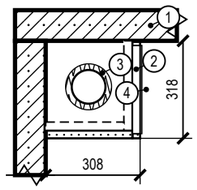

Поз.	Состав слоя, изделие
1	стены существующие — не ослаблять
2	короб: профиль 27×28, ГКЛВ 2×12,5 мм, облицовка плиткой
3	звукоизоляция стояков рулонная 20 мм; К1-1 Ø110
4	ревизионный люк 300×400 мм нажимной, под плитку; против ревизии стояка

4 Гидроизоляция санузла: заход на стены 200 мм, примыкание ванны (М 1:20)


Применение: пом. 6, 7

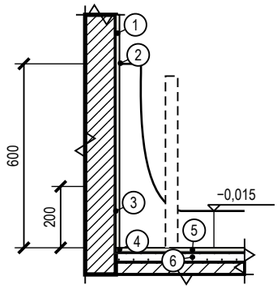

Поз.	Состав слоя, изделие
1	облицовка — плитка на клею С2 TE S1, затирка CG2WA
2	примыкание ванны: лента бордюрная + силиконовый санитарный герметик; облицовка опирается на борт
3	гидроизоляция обмазочная в 2 слоя, заход на стены 200 мм (в зоне душа — выше), до облицовки; акт скрытых работ, тест проливом
4	лента гидроизоляционная в углах и у трапов
5	керамогранит на клею С2 TE S1
6	ЦПС М200 33 мм

5 Плинтус МДФ 69×16 мм у окрашенной стены по доске (ламинату) (М 1:10)


Применение: пом. 1, 2, 3, 8, 9

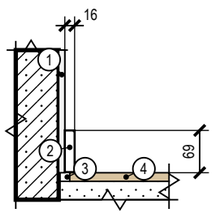

Поз.	Состав слоя, изделие
1	штукатурка, шпаклёвка Q3, окраска — по ведомости отделки
2	плинтус МДФ 69×16 под окраску в цвет стены; клей монтажный — к стене, не к полу
3	зазор покрытия у стены 8–10 мм закрывается плинтусом
4	инженерная доска на клею

6 Плинтус МДФ 69×16 мм у окрашенной стены по керамограниту (плитке) (М 1:10)

Применение: пом. 4, 5

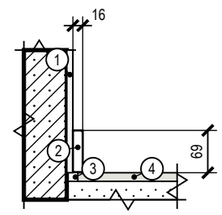

Поз.	Состав слоя, изделие
1	штукатурка, шпаклёвка Q3, окраска — по ведомости отделки
2	плинтус МДФ 69×16 под окраску в цвет стены; клей монтажный — к стене, не к полу
3	зазор покрытия у стены 8–10 мм закрывается плинтусом
4	керамогранит на клею С2 TE S1

Условные обозначения

- железобетон (плита, стены) — условно: конструкция не установлена
- кладка, перегородка — условно: конструкция не установлена
- стяжка, раствор
- гипсокартон ГКЛВ
- звукоизоляция, эластичный заполнитель
- плитка, керамогранит на клею
- инженерная доска (покрытие пола)
- металлический профиль (порог, Т-профиль, короб двери)
- гидроизоляция (обмазочная, лента)

Примечания

1. Узлы — типовые решения проекта для мест, отмеченных выносками на листе схемы расположения развёрток и узлов; размеры — в мм, отметки — в м от ±0,000.
2. Узлы с гидроизоляцией, закладными и коробами скрытого монтажа принимаются по актам скрытых работ до закрытия отделкой; гидроизоляция — после теста проливом (24 ч).
3. Марки изделий (порог, Т-профиль, короб скрытой двери, люк) — по спецификациям; замена — на аналог с теми же габаритами по согласованию с автором проекта.
4. Материал плиты перекрытия и стен в узлах показан условно (железобетон, кладка): конструкция дома не установлена — крепёж, анкеры и толщины слоёв уточняются после обследования (до него — по допущениям общих указаний).


	Лист	№ док.	Подпись	Дата
Дизайнер	Кырлан А.С.			14.11.26
Проверил				
Н. контр.				
Утв.				

Проект: Квартира 65 м²

Узлы	Стадия	Лист	Листов
	П	С13	105

выпуск 14.11.2026 № 3aed0ef730 · стр. 100 из 105

№	Работа	Нед.	После
Р-1	**демонтаж**	1	
Р-2	**контрольный обмер**	0,5	Р-1
Р-3	**перегородки ГКЛ**	0,75	Р-2
Р-4	**черновая электрика**	1,5	Р-3, Р-2
Р-5	черновая сантехника	1	Р-3, Р-2
Р-6	**штукатурка**	2,25	Р-4, Р-5, Р-3
Р-7	**стяжка**	0,75	Р-6
Р-8	**гидроизоляция**	0,5	Р-7
Р-9	ГКЛ	1,5	Р-4, Р-5
Р-10	**плитка**	3	Р-8, Р-9, Р-7
Р-11	**шпаклёвка**	2,5	Р-10, Р-9, Р-6
Р-12	**окраска**	2	Р-11
Р-13	**чистовые полы**	1	Р-12, Р-10
Р-14	**двери и плинтусы**	0,75	Р-13, Р-12
Р-15	**чистовая электрика и сантехника**	1	Р-14, Р-12
Р-16	**кухня и мебель**	1	Р-15, Р-14
Р-17	**сдача**	0,75	Р-16, Р-15
Закупки: заказать не позднее — «◆»; от заказа до поставки — штриховая полоса; срок поставки — только из данных или «ориентир практики»			
З-1	Двери скрытого монтажа с коробом под покраску в существующих проёмах: Д-3, Д-2, Д-5, Д-4	4,25	для Р-6
З-2	Кухонный гарнитур по проекту кухни: модули М-09, М-10, М-11, М-12, М-13, М-14, М-15, М-16	6	для Р-16
З-3	Встраиваемая техника кухни: М-13 холодильник		для Р-16
З-4	Стиральная машина: ОБ-02 (вертикальная загрузка 400 × 600 мм — условие закупки)		для Р-5
З-5	Сантехнические приборы и инсталляции: С-01, С-02, С-03, С-04, С-05		для Р-5
З-6	Керамогранит и плитка: 2 поз. по артикулу и формату, 47,96 м² по раскладке		для Р-10
З-7	Покрытие пола (доска) и плинтус: пом. 1, 2, 3, 8, 9		для Р-13
З-8	Встроенная мебель по замеру цеха: М-17, М-19	6	для Р-16

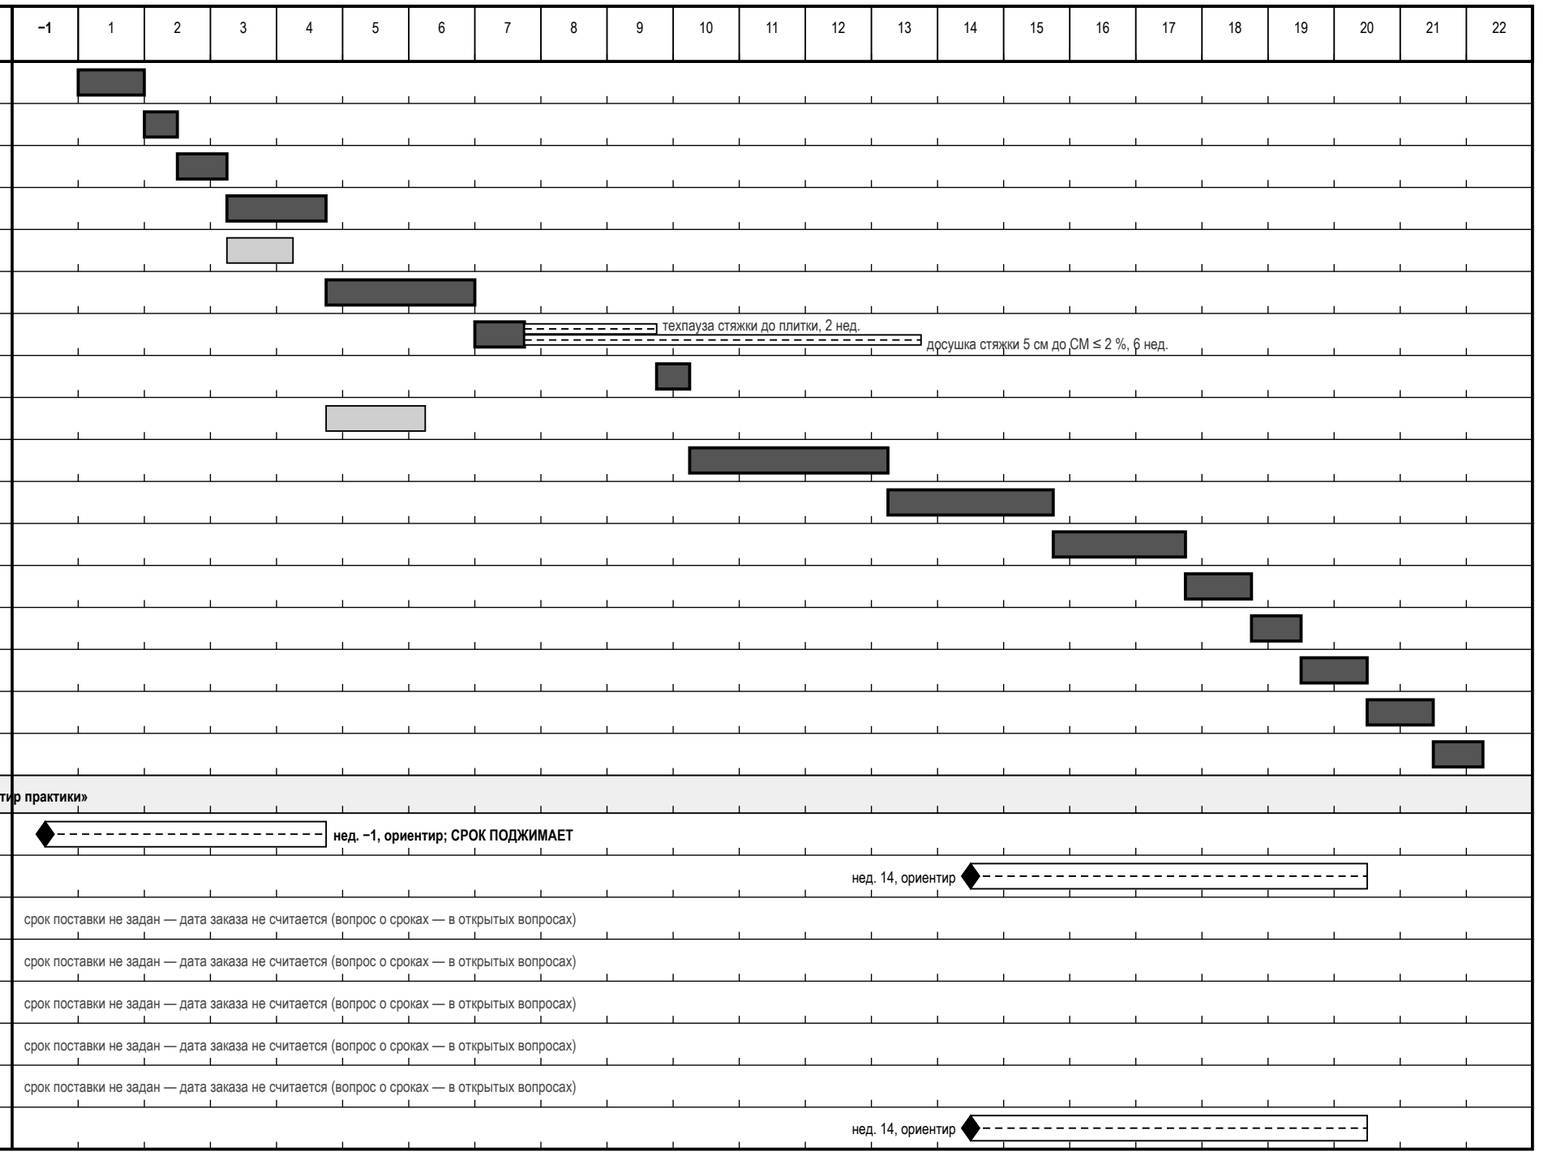

Итого: ≈ 21,25 нед. · жирная линия и тёмная полоса — критический путь

Примечания

1. Длительности этапов — типовые сроки по площади 65,24 м² (таблица «Свод для графика»: недели по этапам для 45, 80 и 120 м², середина вилки, линейная интерполяция); это ориентир, а не норма и не обещание бригады. Контрольный обмер — ориентир 0,5 нед. (в таблице нет).
2. Зависимости «после» — из графика закупок и работ (лист «График закупок и работ»); каждая работа начинается после конца предшественников. Техпаузы стоят отдельными полосами, а не спрятаны в длительности: стяжка → плитка — не менее 2 нед.; стяжка → чистовой пол — досушка стяжки 5 см до СМ ≤ 2 % — 6 нед. (ориентир «1 нед. на 1 см до 4 см, 5 см — 6 нед., 6 см — 8 нед.»; решает замер).
3. График последовательный и поэтому консервативный: в жизни шпаклёвка, плитка и досушка стяжки идут частично параллельно (таблица типовых сроков для 65,24 м²: 14–18 нед.). Совмещения — решение прораба после обмера.
4. Закупки: «заказать не позднее» = начало работы, которой нужна позиция, минус срок поставки. Срок поставки — из данных проекта (срок поставки позиции, срок изготовления обоев в отделке); если его нет, в графике стоит типовой диапазон практики с пометкой «ориентир» — это не срок поставщика, его надо получить до заказа. Кухню и встроенную мебель заказывают после замера по готовым стенам (после штукатурки). Позиции без срока дат заказа не имеют.
5. «Срок поджимает»: самая поздняя дата заказа раньше, чем позицию можно заказать (до замера или обмера): сдвиньте начало работ, ищите изделие с меньшим сроком или заказывайте по предварительному размеру — решение прораба и заказчика.

	Лист	№ док.	Подпись	Дата	Проект: Квартира 65 м²			
Дизайнер	Кырлан А.С.			14.11.26	Календарный график работ и закупок	Стадия	Лист	Листов
Проверил						П	С14	105
Н. контр.								
Утв.								

выпуск 14.11.2026 № 3aed0ef730 · стр. 101 из 105

Приёмка по этапам: контрольные точки, допуски и акты скрытых работ

Этап	Контрольная точка (дальше не пускают без подписи)	Что проверяют	Чем	Допуск	Основание	Подпись	Акт скрытых работ / документ
Р-1	Демонтаж До начала демонтажа: запрошены документы на дом и БТИ	Что снимается и что не трогается: покрытия, отделка, дверные блоки; несущие стены и перегородки — без изменений	осмотр по плану демонтажа	снятое — только по плану; несущее не затрагивать	практика		Фото помещений до и после демонтажа; перечень снятого в журнале работ.
Р-2	Контрольный обмер Контрольный обмер на голых стенах сделан до заказа всего, что делают по размеру	Размеры помещений и проёмов, диагонали, положение стояков, щитка, каналов, толщины стен	рулетка, лазерный дальномер, уровень	допуск задаёт проект; расхождение с планом — в перечень открытых вопросов до заказа	практика		Протокол контрольного обмера с эскизом; расхождения занесены в открытые вопросы.
Р-3	Перегородки ГКЛ Перегородки: разметка против плана монтажа подписана до обшивки	Шаг саморезов: потолок 150 мм; стена 200 мм (лист вертикально) или 300 мм (горизонтально)	рулетка	150 / 200 / 300 мм	практика (СП 163.1325800.2014)		Акт скрытых работ: каркас ГКЛ, закладные под тяжёлое, звукоизоляция в перегородках — до обшивки (фото закладных с привязками); армирование и примыкание к несущим.
		Отступ самореза от кромки и угла листа; расстояние между саморезами на стыке листов	рулетка	5–10 мм от кромки; не менее 15 мм на стыке	практика (СП 163.1325800.2014)		
		Заделка стыков: лента и не менее 2 слоёв шпаклёвки; шляпки утоплены вровень, без прорыва картона	визуально, на просвет	без трещин после высыхания	практика		
		Прогиб каркаса: нет люфта между листом и профилем	простукивание, нажатие рукой	точной цифры нет — сверить перед актом	практика		
Р-4	Черновая электрика Черновая электрика: трассы, высоты подрозетников, замер изоляции подписаны до заделки	Сопротивление изоляции проводки (цепи до 1000 В)	мегаомметр	не менее 0,5 МОм	норматив (ПУЭ, гл. 1.8)		Акт скрытых работ на трассы проводки и слаботочные линии до закрытия штукатуркой и ГКЛ; исполнительная схема трасс с привязками; заземление и уравнивание потенциалов в санузле протокол и фото.
		Целостность и маркировка: PE жёлто-зелёный, N — синий, L — прочие цвета	визуально, прозвонка	каждый проводник промаркирован	практика		
		Высоты подрозетников и привязки — по плану розеток и выключателей	рулетка, уровень	по проекту; от чистого пола	практика		
Р-5	Черновая сантехника Черновая сантехника: опрессовка, отметки выводов, инсталляции подписаны до зашивки	Опрессовка водоснабжения: рабочее давление до 0,6 МПа — испытание 0,9 МПа; выше 0,6 МПа — по расчёту	опрессовочный насос, манометр	выдержка 10 мин (поквартирная); падение: пластик не более 0,06 МПа за 30 мин, сталь не более 0,05 МПа за 10 мин	практика (СП 73.13330)		Акт опрессовки (давление, время, результат); акт скрытых работ на трассы в стенах, полу и коробах; инсталляции, скрытые смесители, трапы — фото с рулеткой и отметками.
		Уклон канализации Ø40–50	уровень, построитель плоскостей	не менее 20 мм на 1 м	норматив (СП 30.13330)		
		Протечки в соединениях, сифоны, смесители, гибкая подводка	осмотр под давлением, салфетка на стыках	нет капель и влажных следов в контрольное время	практика		
		Отметки выводов и положение инсталляций до зашивки и гидроизоляции	рулетка в кадре, фото	по листу выводов	практика		
Р-6	Штукатурка Маяки стен проверены до штукатурки; коробки скрытых дверей стоят до штукатурки	Отклонение от вертикали (простая / улучшенная / высококачественная штукатурка)	отвес, лазерный уровень	3 / 2 / 1 мм на 1 м; не более 15 / 10 / 5 мм на высоту	практика (СП 71.13330.2017)		Фото коробок скрытых дверей с отметкой чистого пола — до штукатурки; класс штукатурки (простая / улучшенная / высококачественная) назван в договоре.
		Отклонение от горизонтали	уровень, правило	3 / 2 / 1 мм на 1 м; не более 15 / 10 / 5 мм на длину	практика (СП 71.13330.2017)		
		Неровности (плоскостность)	правило 2 м и щуп	до 5 / 3 / 2 мм на 1 м; не более 3 / 2 / 2 неровностей на 4 м²	практика (СП 71.13330.2017)		
		Влажность основания перед шпаклёвкой и отделкой	влагомер	верхние 20–30 мм — не более 5 % по массе	норматив (СП 71, табл. 7.2)		

	Лист	№ док.	Подпись	Дата	Проект: Квартира 65 м²			
Дизайнер	Кырлан А.С.			14.11.26				
Проверил					Чек-лист приёмки по этапам. Лист 1 из 3	Стадия	Лист	Листов
Н. контр.						П	С15	105
Утв.								

Приёмка по этапам: контрольные точки, допуски и акты скрытых работ (продолжение)

Этап	Контрольная точка (дальше не пускают без подписи)	Что проверяют	Чем	Допуск	Основание	Подпись	Акт скрытых работ / документ
Р-7	Стяжка Стяжка: подготовка, после заливки ровность, затем замер СМ перед чистовым полом	Ровность: просвет под рейкой 2 м	рейка 2 м, клиновой щуп	под паркет, ламинат — 2 мм; под гидроизоляцию до 4 мм; прочие покрытия — до 6 мм (цифры расходятся между источниками — сверить перед актом)	практика (СП 29.13330)		Акт скрытых работ на стяжку (толщина, армирование) до чистового пола; протокол ровности и протокол СМ-влажности; звукоизоляция и демпферная лента под стяжкой — фото и паспорт; контуры тёплого пола до заливки — схема укладки и замер сопротивления.
		Отклонение от горизонтали по помещению	уровень, нивелир	не более 0,2 % длины помещения	практика (СП 29.13330)		
		Число точек измерения	рейка	не менее 3 на 30 м² или 1 на небольшое помещение	практика		
		Отслоения и пустоты	простукивание молотком или киянкой	глухой звук — зона вскрывается и переделывается	практика		
		Влажность перед укладкой доски: цементная стяжка	влагомер; СМ-замер	ЦПС не более 2,0 % СМ (с тёплым полом не более 1,8 %); влагомер для плитки — не более 5 %	практика (СП 71; рекомендации производителей)		
Р-8	Гидроизоляция Гидроизоляция: пролив 24 ч подпись до плитки	Заведение на стены не ниже 200 мм от чистого пола; за ванной — 300 мм выше борта; в душе без поддона — на высоту лейки	рулетка	не менее 200 мм	норматив (СП 71.13330.2017, п. 8.6.5); остальное — практика		Акт теста проливом, фото узлов и высоты заведения на стены — до плитки.
		Тест проливом: слой воды 10–30 мм, контроль уровня и потолка соседа снизу	линейка, визуально	24 ч (минимум 12 ч); падения уровня и протечки нет	практика		
		Два слоя обмазки с межслойной сушкой, лента в углах и манжеты на выводах	визуально	по инструкции производителя	практика		
Р-9	ГКЛ Короба, ниши и потолки: черновые сети в зоне коробов приняты до обшивки	Шаг саморезов, отступ от кромки, заделка стыков (как у перегородок)	рулетка, визуально	потолок 150 мм; кромка 5–10 мм; стык — лента и 2 слоя шпаклёвки	практика (СП 163.1325800.2014)		Акт скрытых работ: каркас ГКЛ, закладные, звукоизоляция — фото до обшивки; воздуховоды в коробах и за потолком — фото и схема.
		Закладные под тяжёлое, карнизы, подвесные светильники на месте до обшивки	фото с привязками	по плану потолков и узлам	практика		
		Ревизионные люки: доступ к арматуре и ревизиям сохранён	осмотр	по листу ВК	практика		
Р-10	Плитка Раскладка плитки: первая плита и первый ряд проверены по развёртке; плитка выбрана, калибр партии измерен	Уступы между смежными плитками	линейка, на просвет	не более 1 мм	норматив (СП 71.13330.2017)		Раскладка подписана до начала плитки; протокол первого ряда; акт теста проливом приложен (этап гидроизоляции).
		Ширина шва и его прямолинейность	линейка, калибр	до 6 мм ручная укладка; фактическая по проекту ±0,5 мм	практика		
		Отклонение рядов от вертикали и горизонтали	уровень, правило, отвес	1,5 мм на 1 м длины	практика		
		Ровность облицовки	правило 2 м и щуп	не более 2–4 мм (цифра расходится по источникам)	практика		
		Пустоты под плиткой	простукивание всей площади	до 10 % площади допустимо; свыше 25 % под одной плиткой — брак	практика		
Р-11	Шпаклёвка Шпаклёвка Q3/Q4: проверка боковым светом до окраски	Класс основания под окраску: Q3 — сплошное финишное шпаклевание; Q4 — под направленный свет	переносной прожектор у поверхности под острым углом	Q3: царапины от абразива до 0,5 мм; Q4 — без видимых царапин и теней; неровность на 2 м: Q3 — 1 мм, Q4 — 0,5 мм	практика (Q-классы — не норматив СП, а согласованный критерий)		Класс (Q3 или Q4) назван в договоре; грунтование и армирование стыков перед шпаклёвкой — запись в журнале.
Р-12	Окраска Выкрасы утверждены, колеровка одной партией	Окраска без полос, подтёков, пропусков; цвет — по колерной карте	боковой свет, образец выкраса	без видимых дефектов при боковом свете	практика		Утверждённые выкрасы; остаток колеровки одной партии — для подкраски.

	Лист	№ док.	Подпись	Дата
Дизайнер	Кырлан А.С.			14.11.26
Проверил				
Н. контр.				
Утв.				

Проект: Квартира 65 м²

Чек-лист приёмки по этапам. Лист 2 из 3

Стадия	Лист	Листов
П	С16	105

Приёмка по этапам: контрольные точки, допуски и акты скрытых работ (продолжение)

Этап	Контрольная точка (дальше не пускают без подписи)	Что проверяют	Чем	Допуск	Основание	Подпись	Акт скрытых работ / документ
		Основание сухое, огрунтованное; защита от прямого солнца при высыхании	осмотр	по ТУ краски	норматив (СП 71.13330.2017, п. 7.5.2)		
Р-13	Чистовые полы Чистовые полы: влажность, ровность, уступы, зазоры — до укладки доски; мокрые работы закончены	Деформационный зазор у стен и порогов (доска, ламинат)	линейка, клинья при укладке	8–15 мм (чаще 10 мм); у ламината 5–10 мм по СП 71	практика (требования производителей); норматив (СП 71, п. 8.10.14)		Протокол СМ-влажности стяжки до укладки; паспорт и партия доски.
		Перепад основания под покрытие	правило 2 м и щуп	не более 2 мм на 2 м	практика		
		Зазоры и перепады между досками; скрип; видимый зазор в замке — брак	щуп, рука, шаг	«ступеньки» нет	практика		
		Влажность помещения при укладке и после	гигрометр	не более 60 %, без сквозняков	норматив (СП 71, п. 8.1.7)		
Р-14	Двери и плинтусы Полотна и плинтусы — после чистового пола; скрытые полотна после чистовой отделки стен	Отклонение коробки от вертикали	отвес, уровень	1,5 мм на 1 м, не более 3 мм на коробку	практика (ТР 105-00, пересказ)		Коробки скрытых дверей приняты до штукатурки (этап штукатурки); паспорт на полотна.
		Зазор между полотном и коробкой по периметру	щуп	2–4 мм по бокам и верху (единого норматива нет)	практика		
		Открывание и закрывание: без перекоса, плавный ход петель и доводчика	визуально, от руки	без задевания коробки и пола	практика		
Р-15	Чистовая электрика и сантехника Чистовая электрика и сантехника: протокол электролаборатории и проверка УЗО до подписи акта	УЗО: кнопка «Тест»; время отключения; ток отключения	кнопка на аппарате; прибор проверки УЗО (не мультиметр)	отключает; не более 0,3 с; 50–100 % от IΔn	практика измерений		Протокол измерений аккредитованной электролаборатории (изоляция по группам, УЗО, PE, фаза-ноль); исполнительная схема щита; акт опрессовки приложен (этап ВК).
		Сопротивление изоляции готовых линий; петля фаза-ноль для срабатывания автоматов	мегаомметр; прибор петли фаза-ноль	изоляция не менее 0,5 МОм; петля — по проекту	норматив (ПУЭ, гл. 1.8) / по проекту		
		Смесители, сифоны, гибкая подводка: пробный пуск воды	визуально под нагрузкой	нет подтёков в контрольное время	практика		
Р-16	Кухня и мебель Кухня и мебель: замер кухни снят по готовым стенам; чистовая электрика и сантехника подведены	Привязка выводов и розеток к модулям кухни; вытяжка, вентиляция	рулетка, сверка с листом кухни	по проекту кухни	практика		Акт передачи кухни; паспорта техники и гарантийные талоны.
		Тяга вентиляции у решёток	лист бумаги у решётки	бумага притягивается; при сомнениях — замер анемометром	практика		
Р-17	Сдача Финальная приёмка по таблицам СП 71: дефектная ведомость и акт	Стены, потолки, полы, плитка, двери, окна осмотр по чек-листу этапов выше	правило 2 м, уровень, щуп, боковой свет, влагомер	по таблицам выше	практика		Дефектная ведомость и акт приёмки; гарантия: по умолчанию претензии по качеству работ — 2 года, в договоре прописывается отдельно.
		Полный пакет документов: акты скрытых работ, протокол электролаборатории, акт опрессовки, исполнительные схемы, гарантийные обязательства	комплектность	пакет собран до подписи акта	практика		

Примечания

1. Метка основания: «норматив» — цифра подтверждена текстом СП, ГОСТ или ПУЭ; «практика» — отраслевая конвенция или один источник: к спору не годится без сверки первоисточника (СП 71.13330.2017, СП 29.13330, СП 163.1325800.2014, ПУЭ гл. 1.8, СП 73.13330, СП 30.13330).
2. Класс штукатурки (простая / улучшенная / высококачественная) и класс основания под окраску (Q3 или Q4) называются в договоре подряда: допуск выбирается по ним. Q-классы — не норматив, а согласованный сторонами критерий.
3. Акт скрытых работ подписывают до того, как работа закрыта следующим слоем (штукатуркой, плиткой, стяжкой, обшивкой): постфактум он слабее — осматривать нечего. Подписывают заказчик (или технадзор), подрядчик; при перепланировке — автор проекта. Каждую зону снимают до закрытия с рулеткой в кадре и привязкой к стене.
4. По умолчанию, если срок не прописан в договоре, претензии по качеству работ можно предъявить в течение 2 лет со дня приёмки; в договоре гарантийный срок и сроки на скрытые работы рекомендуется назвать явно.

	Лист	№ док.	Подпись	Дата	Проект: Квартира 65 м²			
Дизайнер	Кырлан А.С.			14.11.26	Чек-лист приёмки по этапам. Лист 3 из 3	Стадия	Лист	Листов
Проверил						П	С17	105
Н. контр.								
Утв.								

Какому мастеру какие листы (номера — как в штампе)

Мастер	Что делает по альбому	Листы	Кроме чертежей — документы	Листов
Замерщик и прораб (до начала работ)	Контрольный обмер на голых стенах, сверка размеров и диагоналей, ответы на открытые вопросы до заказа	14, 16, 81–82	Задание на контрольный обмер; лист открытых вопросов	4
Гипсокартонщик и монтажник перегородок	Демонтаж и возведение перегородок, каркас, короба инсталляции, ниши, потолки; закладные под навесное	17–19, 40–42	Ведомость материалов каркаса; акт скрытых работ на каркас	6
Электрик	Группы щита, подрозетники и высоты, трассы, свет, управление светом, слаботочка, тёплый пол	43–50, 56–80	Таблица нагрузок; ведомость изделий; протокол электролаборатории	33
Сантехник	Выводы воды и канализации, разводка, аксонометрии, инсталляции, короба стояков	27–35, 56–80	Спецификация ВК; акт опрессовки; акт пролива	34
Монтажник вентиляции, отопления и кондиционеров	Вентиляция, радиаторы и тёплые полы, кондиционеры: места, размеры, трассы и дренаж	51–52	Акт опрессовки азотом (кондиционеры); фото воздуховодов до закрытия	2
Штукатур, шпаклёвщик, маляр, паркетчик	Основание стен, окраска и обои по колерной карте, полы и пороги, плинтус, узлы стыков	20–21, 53, 56–80, С1–С3, С13	Колерная карта и выкрасы; спецификация отделочных материалов	32
Плиточник	Раскладка и подрезка плитки стен, пола и фартука, гидроизоляция, швы, выводы в плитке	32–34, 36–37, 54–80, С13	Ведомость плитки; акт теста проливом	33
Монтажник дверей и окон	Заполнение проёмов: размеры коробок, открывание, пороги, скрытые двери	38–39	Ведомость проёмов; паспорта на полотна	2
Мебельщик, кухонный монтажник	Кухня и мебель на заказ: габариты, членение, фурнитура, связка с электрикой и сантехникой	18–19, 22–26, Д1–Д5	Ведомость изделий; замер кухни по готовым стенам	12
Заказчик и комплектатор	Что и когда покупать, сколько с запасом, во что это обойдётся; свет, декор и текстиль; визуализации как должно получиться	1–13, 15, 49, С4–С12, С14	Список покупок; смета; календарный график	25
Прораб и технадзор (приёмка)	Приёмка этапов, акты скрытых работ, дефектная ведомость	С14–С18	Чек-лист приёмки по этапам; календарный график	5

Примечания

1. Номера листов — как в основной надписи: основные подряд (1, 2, 3…), «Д» — детализация мебели, «С» — ведомости, спецификации, узлы и сметы, «П» — приложение единого комплекта. «12–18» — все листы с 12 по 18.
2. Лист может быть у нескольких мастеров: развёртка стены нужна электрику (высоты точек), сантехнику (выводы), отделочнику (материалы) и плиточнику (раскладка). Общие листы (обмер, список листов, перечень вопросов) прораб раздаёт всем.
3. Мастер работает по чертежам и берёт в руки то, что назначено ему здесь; закупки, смету и график ведёт заказчик с прорабом. Лист, которого нет в таблице ни у одного мастера, — вопрос прорабу: чей он.

	Лист	№ док.	Подпись	Дата	Проект: Квартира 65 м²			
Дизайнер	Кырлан А.С.			14.11.26	Лист → мастер	Стадия	Лист	Листов
Проверил						П	С18	105
Н. контр.								
Утв.								