
L

LINEA

ДИЗАЙН-ПРОЕКТ ИНТЕРЬЕРА

Четырёхкомнатная квартира

13 помещений

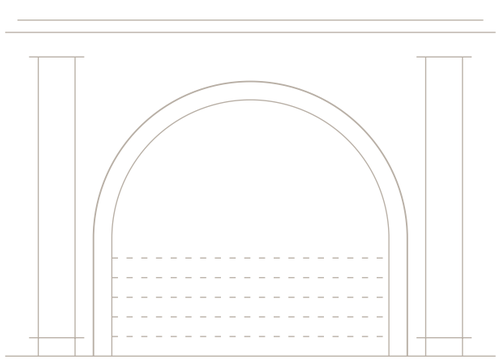

ПАЛИТРА ОТДЕЛКИ

F497	J484	L481	V486	NCS S 3005-Y20
82 %	12 %	6 %	текстиль, декор	текстиль, декор

АВТОР ПРОЕКТА

Кырлан Александр Сергеевич

Ноябрь 2026



Визуализация гостиной · 3D

ОБЩАЯ ПЛОЩАДЬ	ПОМЕЩЕНИЙ	СТАДИЯ	ШИФР	ОСНОВА
102,67 м²	13, из них жилых 4	Проект · предварительно	ГД-2026-004-АИ	план заказчика, без обмера

Как оставить правку: кнопка «Правка к этому листу» в правом верхнем углу любого листа · все листы проекта: дизайн-студия-квартир.рф/review.html?p=gost-proekt2

выпуск 14.11.2026 № e7147312ff · стр. 1 из 147

Объект

Четырёхкомнатная квартира: 106,37 м², помещений 13, из них жилых 4.

Стиль: современный (контемпорари) 100 %. Стадия: предварительный альбом без обмера, планировка по плану заказчика.

Открытых вопросов 28, конфликтов разделов 1; изменений утверждено 21, ждут подписи 1.

Розетки и выводы

49 розеток (рамок 38), 5 выводов кабеля под технику и свет, 19 групп щита — всё с высотами от чистого пола: листы 56, 57, 60.

Что решено (подписано вами)

ИЗ-1 — Окно на наружной стене В (1580…3080.

ИЗ-2 — Добавлены: бра Св63 у изголовья кровати М-35 (стена А, смещение 510, высота 1400 мм, 6 Вт, 2700 К, линия L21) и выключатель S17 (стена А, смещение 1050…

ИЗ-3 — Добавлен светильник Св64 над зеркалом ДК17 (стена Б, смещение 600, высота 1950 мм, 8 Вт, 3000 К, IP44, драйвер встроен, линия L12, группа 4).

и ещё 18 — на листе реестра

Предложено, ждёт подписи: ИЗ-22

Что ждёт вашего ответа

вопросов 29; блокируют заказ или работы — 8, они первыми и выделены

№	Вопрос	Варианты · что будет без ответа	Нужен ответ
К-21	Все размеры сняты с размерных цепочек растрового скана заказчика, контрольного обмера нет.	Без ответа: Размеры и площади остаются ориентировочными; штамп печатает «Общая площадь 102,67 м²» как расчётную величину, не подтверждённую обмером; до обмера не заказывать материалы и изделия по размерам листов.	**до заказа мебели и материалов**
К-24	Высота потолка 2700 мм принята: источника (замер, проект дома) в материалах объекта нет.	Без ответа: Высота 2700 мм остаётся принятой, не замеренной: вертикальные размеры листов и объёмы работ ориентировочные; встроенную мебель и плитку по высоте не заказывать до замера.	**до заказа мебели и материалов**
К-27	Модели встраиваемой техники кухни не выбраны: холодильник (М-19), духовой шкаф (М-21) и посудомоечная машина (М-26) заданы описанием «аналог по характеристикам» — без…	Без ответа: ниши остаются по типовой схеме на 600 мм, не подтверждённой паспортом модели; модули кухни не заказывать до выбора техники.	**До заказа модулей кухни**
К-28	Санузел (пом. 10): унитаз С-06 при положении стояков по данным имеет выпуск 3600 мм до стояка К1 и 2357 мм до стояка Ø110 по прямой (,…		**до начала этих работ**
К-29	Мойка кухонная С-05 (пом. 6 «Кухня»), выпуск К1-5 Ø50: в полу не помещается: врезка + перепад 202 (10,10 м × 20 мм/м) + Ø50 + слой над трубой 45 = 307 мм при пироге 170 мм.	Решить: (а) подиум или подъём пола на 140 мм (ступень на входе — порог); (б) прибор ближе к стояку Ст К1-2; (в) насосная установка (КНС) у прибора — по паспорту, требует согласования. Без ответа: выпуск К1-5 и кухню в…	**до начала этих работ**
К-30	Посудомоечная машина ОБ-03 (пом. 6 «Кухня»), выпуск К1-6 Ø50: в полу не помещается: врезка + перепад 152 (7,60 м × 20 мм/м) + Ø50 + слой над трубой 45 = 257 мм при пироге 170 мм.	Решить: (а) подиум или подъём пола на 90 мм (ступень на входе — порог); (б) прибор ближе к стояку Ст К1-2; (в) насосная установка (КНС) у прибора — по паспорту, требует согласования. Без ответа: выпуск К1-6 и кухню в…	**до начала этих работ**
К-31	Гостиная (пом. 11, 14,55 м²) в данных без двери и проёма: со всех сторон глухие стены (к детской 1 — стена А, к детской 2 — стена Г, к гардеробной 1 — стена Б), единственная…	Без ответа: гостиная и гардеробная 1 недостижимы: отделку, потолок, ЭОМ и мебель в них не выполнять; если вход через детскую 2, расстановку детской 2 пересматривать.	**до начала этих работ**
К-32	Помещение «Детская 1»: выключатель основного света L13 не у входа — свет включают только прикроватные выключатели (S3), выключателя у входа нет.	Варианты: (а) петли на другую сторону — ручка уходит от угла, выключатель встаёт у ручки; (б) шкаф или тумбу у двери сдвинуть на 300 мм — место освобождается; (в) проходной выключатель у входа в пару к прикроватному…	**до выпуска рабочей документации**
К-1	Окно детской 2 (поз. 9) на наружной стене В: привязки 1580…3080 в источниках нет — в экспликации скана окна этой комнаты не показано.	Без ответа: Остаётся принятое положение окна как допущение, не замер. Конфликт со стояками Кф-1 не снят: радиатор под окном, шторы и короб со стояками на этом месте не совмещаются.	до выпуска рабочей документации
К-3	Несущие стены не определены (нет плана БТИ и техзаключения): до их получения демонтаж не планируется.	Без ответа: действует принятое на листах.	До любого демонтажа и штробления в стенах
К-4	Гостиная (поз. 11): мебели в модели нет, расстановка ждёт решения заказчика.	Без ответа: действует принятое на листах.	до выпуска рабочей документации
К-5	Гардеробная 1 (поз. 12) в натуре трапеция 2320/2132/1400, в модели прямоугольник той же площади: нужен контрольный обмер углов.	Без ответа: действует принятое на листах.	до выпуска рабочей документации
К-6	Розетка Р7 (стиральная машина, ванная комната) стоит в 72 мм от угла при норме от 150 мм.	Без ответа: Р7 остаётся на 2543 мм вдоль стены и 949 мм по высоте, в 72 мм от угла: замечание открыто.	до выпуска рабочей документации
К-7	Акцент L481 занимает больше порога 15 % площади поверхностей на акцентной стене А Гостиной — 16 % (проверка по доле акцента, замечание открыто намеренно).	Без ответа: Остаётся акцентная стена L481 в Гостиной, доля 16 % выше порога 15 %; замечание открыто.	до выпуска рабочей документации
К-8	Графы «Пров.» и «Н. контр.» в штампе пусты: их заполняет человек, подписи проверяющего и нормоконтролёра автор проекта не ставит.	Без ответа: графы остаются пустыми; комплект предварительный, не проверен независимо.	до выпуска рабочей документации
К-10	Прямые углы помещений с кухней, санузлами, гардеробными и встроенной мебелью по скану не подтверждены (скос стен приведён к ступеням): ванная комната, тёмная комната, детская…	Без ответа: действует принятое на листах.	до выпуска рабочей документации
К-12	Состав подрядчиков и поставщиков (кто покупает и кто монтирует радиаторы, подоконники, двери, розетки) от заказчика не получен.	Без ответа: остаётся типовая схема: покупает заказчик, монтирует подрядная бригада, скрытые работы принимает автор; закрепление за конкретными подрядчиками не подтверждено.	до заказа мебели и материалов
К-13	Детская 2: рабочий стол М-37 у стены Б получает боковой свет от окна справа от сидящего.	Без ответа: действует принятое на листах.	до выпуска рабочей документации
К-14	Из чего стены под навесными шкафами — Ванная комната (стена Б, М-07), Кухня (стена А, М-23, М-24, М-25), Гардеробная 2 (стена В, М-34)? Проекта дома нет, на скане материал и…	Без ответа: действует принятое на листах.	до выпуска рабочей документации
К-15	Стояки Ст К1-2 и Ст В1-2 (в данных (9400.	Без ответа: Остаются принятые положения окна и стояков без замера; радиатор под окном, шторы и короб со стояками на этом месте не совмещаются.	до выпуска рабочей документации
К-17	Ведущий цвет — Paper F497 на стенах и потолке — занимает больше 80 % площади поверхностей в Тёмной комнате (87 %), Гардеробной 2 (89 %), Гардеробной 1 (86 %) и Балконе 1 (85…	Без ответа: Остаются цвета автора: стены и потолок в Paper F497, доля ведущего цвета 85–89 %.	до выпуска рабочей документации
К-18	Вытяжка М-24 встроена в навесной модуль на отметке 1550 мм: её низ над электрической варочной панелью 610 мм, а фартук 650 мм при практике 450–600 мм.	Без ответа: Остаётся модуль на отметке 1550 мм; низ вытяжки 610 мм над панелью, меньше 650 мм; допустимость высоты не подтверждена.	До заказа модулей М-23, М-24, М-25
К-19	Привязка угла помещения «Гостиная» (поз.	Без ответа: Остаётся угол в точке (10670; 3470) как допущение: размеры правой части на листах — расчётные, возможен сдвиг до ≈700 мм; мебель, свет и розетки там привязаны к принятым координатам.	до выпуска рабочей документации
К-20	Наружные скошенные стены (в натуре под 45°) заменены на планах ступенями: движок описывает только ортогональную геометрию.	Без ответа: Остаются ступени вместо скоса: фактическая форма наружных стен Гостиной и Гардеробной 1 на листах не показана, размеры вдоль скоса брать по обмеру на месте.	до выпуска рабочей документации
К-22	Окно Гостиной (пом. 11) на стене В, часть 2: остекление показано по обмерному скану, размеры 1500×1600 мм и подоконник 900 мм приняты типовыми, не замерены.	Без ответа: Остаются типовые размеры окна 1500×1600 мм, подоконник 900 мм; на плане они напечатаны как принятые, не замеренные.	до выпуска рабочей документации

Показано 25 из 29; остальные и полный текст каждого вопроса — на листах 107, 108, 109, 110, 111, 112 реестра открытых вопросов.

	Лист	№ док.	Подпись	Дата	Проект: Четырёхкомнатная квартира			
Дизайнер	Кырлан А.С.			14.11.26	Ваш проект на одной странице	Стадия	Лист	Листов
Проверил						П	2	147
Н. контр.								
Утв.								



	Лист	№ док.	Подпись	Дата	Проект: Четырёхкомнатная квартира			
Дизайнер	Кырлан А.С.			14.11.26				
Проверил					Визуализация: Зал	Стадия	Лист	Листов
Н. контр.								
Утв.						П	3	147

выпуск 14.11.2026 № e7147312ff · стр. 3 из 147



	Лист	№ док.	Подпись	Дата	Проект: Четырёхкомнатная квартира			
Дизайнер	Кырлан А.С.			14.11.26				
Проверил					Визуализация: Зал	Стадия	Лист	Листов
Н. контр.								
Утв.						П	4	147

выпуск 14.11.2026 · e7147312ff · стр. 4 из 147



	Лист	№ док.	Подпись	Дата
Дизайнер	Кырлан А.С.			14.11.26
Проверил				
Н. контр.				
Утв.				

Проект: Четырёхкомнатная квартира

Визуализация: Зал	Стадия	Лист	Листов
	П	5	147

выпуск 14.11.2026 № e7147312ff · стр. 5 из 147



	Лист	№ док.	Подпись	Дата	Проект: Четырёхкомнатная квартира			
Дизайнер	Кырлан А.С.			14.11.26				
Проверил					Визуализация: Зал	Стадия	Лист	Листов
Н. контр.								
Утв.						П	6	147

выпуск 14.11.2026 · e7147312ff · стр. 6 из 147



	Лист	№ док.	Подпись	Дата	Проект: Четырёхкомнатная квартира			
Дизайнер	Кырлан А.С.			14.11.26				
Проверил					Визуализация: Ванная комната	Стадия	Лист	Листов
Н. контр.								
Утв.						П	7	147

выпуск 14.11.2026 · e7147312ff · стр. 7 из 147



	Лист	№ док.	Подпись	Дата	Проект: Четырёхкомнатная квартира			
Дизайнер	Кырлан А.С.			14.11.26				
Проверил					Визуализация: Тёмная комната	Стадия	Лист	Листов
Н. контр.								
Утв.						П	8	147



	Лист	№ док.	Подпись	Дата	Проект: Четырёхкомнатная квартира			
Дизайнер	Кырлан А.С.			14.11.26				
Проверил					Визуализация: Детская 1	Стадия	Лист	Листов
Н. контр.								
Утв.						П	9	147

выпуск 14.11.2026 № e7147312ff · стр. 9 из 147



	Лист	№ док.	Подпись	Дата	Проект: Четырёхкомнатная квартира			
Дизайнер	Кырлан А.С.			14.11.26				
Проверил					Визуализация: Детская 1	Стадия	Лист	Листов
Н. контр.								
Утв.						П	10	147



	Лист	№ док.	Подпись	Дата
Дизайнер	Кырлан А.С.			14.11.26
Проверил				
Н. контр.				
Утв.				

Проект: Четырёхкомнатная квартира

Визуализация кухни	Стадия	Лист	Листов
	П	11	147



	Лист	№ док.	Подпись	Дата
Дизайнер	Кырлан А.С.			14.11.26
Проверил				
Н. контр.				
Утв.				

Проект: Четырёхкомнатная квартира

Визуализация кухни	Стадия	Лист	Листов
	П	12	147

выпуск 14.11.2026 № e7147312ff · стр. 12 из 147



	Лист	№ док.	Подпись	Дата	Проект: Четырёхкомнатная квартира			
Дизайнер	Кырлан А.С.			14.11.26				
Проверил					Визуализация: Прихожая-коридор	Стадия	Лист	Листов
Н. контр.								
Утв.						П	13	147

выпуск 14.11.2026 № e7147312ff · стр. 13 из 147



	Лист	№ док.	Подпись	Дата	Проект: Четырёхкомнатная квартира			
Дизайнер	Кырлан А.С.			14.11.26				
Проверил					Визуализация: Гардеробная 2	Стадия	Лист	Листов
Н. контр.								
Утв.						П	14	147



	Лист	№ док.	Подпись	Дата	Проект: Четырёхкомнатная квартира			
Дизайнер	Кырлан А.С.			14.11.26				
Проверил					Визуализация: Детская 2	Стадия	Лист	Листов
Н. контр.								
Утв.						П	15	147

выпуск 14.11.2026 № e7147312ff · стр. 15 из 147



	Лист	№ док.	Подпись	Дата
Дизайнер	Кырлан А.С.			14.11.26
Проверил				
Н. контр.				
Утв.				

Проект: Четырёхкомнатная квартира

Визуализация санузла	Стадия	Лист	Листов
	П	16	147



	Лист	№ док.	Подпись	Дата	Проект: Четырёхкомнатная квартира			
Дизайнер	Кырлан А.С.			14.11.26				
Проверил					Визуализация гостиной	Стадия	Лист	Листов
Н. контр.								
Утв.						П	17	147

выпуск 14.11.2026 № e7147312ff · стр. 17 из 147



	Лист	№ док.	Подпись	Дата	Проект: Четырёхкомнатная квартира			
Дизайнер	Кырлан А.С.			14.11.26				
Проверил					Визуализация: Гардеробная 1	Стадия	Лист	Листов
Н. контр.								
Утв.						П	18	147

выпуск 14.11.2026 № e7147312ff · стр. 18 из 147

Список листов

Лист	Наименование
1	Титульный лист
2	Ваш проект на одной странице
3	Визуализация: Зал
4	Визуализация: Зал
5	Визуализация: Зал
6	Визуализация: Зал
7	Визуализация: Ванная комната
8	Визуализация: Тёмная комната
9	Визуализация: Детская 1
10	Визуализация: Детская 1
11	Визуализация кухни
12	Визуализация кухни
13	Визуализация: Прихожая-коридор
14	Визуализация: Гардеробная 2
15	Визуализация: Детская 2
16	Визуализация санузла
17	Визуализация гостиной
18	Визуализация: Гардеробная 1
19	Список листов
20	Список листов
21	Как читать альбом
22	План планировки от заказчика
23	План монтажный
24	Кухня (пом. 6). Монтажная схема
25	Кухня (пом. 6). Монтажная схема
26	Шкафы. Монтажная схема. Лист 1 из 3
27	Шкафы. Монтажная схема. Лист 2 из 3
28	Шкафы. Монтажная схема. Лист 3 из 3
29	Карта покрытий стен
30	Колерная карта
31	Колерная карта
32	План размещения мебели и оборудования
33	Спецификация мебели и оборудования
34	Спецификация мебели и оборудования (продолжение)
35	Спецификация мебели и оборудования (продолжение)
36	Спецификация мебели и оборудования (продолжение)
37	Спецификация мебели и оборудования (продолжение)
38	Ведомости изделий, техники и фурнитуры
39	План выводов сантехники
40	Схема разводки водопровода и канализации
41	Аксонометрическая схема В1 (холодное водоснабжение)
42	Аксонометрическая схема Т3 (горячее водоснабжение)
43	Аксонометрическая схема К1 (канализация)
44	Развёртки мокрых зон: выводы ВК. Ванная комната
45	Развёртки мокрых зон: выводы ВК. Санузел
46	Спецификация сантехнического оборудования
47	Раскладка плитки. Ванная комната. Развёртки стен
48	Раскладка плитки. Санузел. Развёртки стен
49	План размещения дверей
50	Ведомость заполнения проёмов
51	План потолков
52	Разрезы и узлы потолков
53	Разрезы и узлы потолков (продолжение)
54	Сечения потолков М 1:10
55	Сечения потолков М 1:10
56	Однолинейная схема щита
57	Однолинейная схема щита (продолжение)
58	Таблица нагрузок щита
59	План принципиальных трасс
60	План розеток и электровыводов
61	План слаботочных сетей
62	План освещения
63	Техническое задание на подбор светильников
64	Управление светильниками
65	План вентиляции
66	План отопления
67	План покрытий пола
68	Раскладка плитки. Планы полов
69	Раскладка плитки. Фартук кухни
70	Развёртка стены А. Зал (пом. 1)
71	Развёртка стены Б. Зал (пом. 1)
72	Развёртка стены В. Зал (пом. 1)
73	Развёртка стены Г. Зал (пом. 1)
74	Развёртка стены А. Ванная комната (пом. 2)

	Лист	№ док.	Подпись	Дата	Проект: Четырёхкомнатная квартира			
Дизайнер	Кырлан А.С.			14.11.26	Список листов	Стадия	Лист	Листов
Проверил						П	19	147
Н. контр.								
Утв.								

выпуск 14.11.2026 № e7147312ff · стр. 19 из 147

Список листов (продолжение)

Лист	Наименование
75	Развёртка стены Б. Ванная комната (пом. 2)
76	Развёртки стен В, Г. Ванная комната (пом. 2)
77	Развёртки стен А, Б. Тёмная комната (пом. 3)
78	Развёртки стен В, Г. Тёмная комната (пом. 3)
79	Развёртка стены А. Детская 1 (пом. 4)
80	Развёртка стены Б. Детская 1 (пом. 4)
81	Развёртка стены В. Детская 1 (пом. 4)
82	Развёртка стены Г. Детская 1 (пом. 4)
83	Развёртка стены А. Коридор (пом. 5)
84	Развёртка стены В. Коридор (пом. 5)
85	Развёртка стены А. Кухня (пом. 6), кухонный фронт
86	Развёртка стены Б. Кухня (пом. 6)
87	Развёртка стены В. Кухня (пом. 6)
88	Развёртка стены Г. Кухня (пом. 6)
89	Развёртка стены А. Прихожая-коридор (пом. 7)
90	Развёртка стены Б. Прихожая-коридор (пом. 7)
91	Развёртки стен В, Г. Прихожая-коридор (пом. 7)
92	Развёртки стен А, Б, Г. Гардеробная 2 (пом. 8)
93	Развёртка стены В. Гардеробная 2 (пом. 8)
94	Развёртка стены А. Детская 2 (пом. 9)
95	Развёртка стены Б. Детская 2 (пом. 9)
96	Развёртка стены В. Детская 2 (пом. 9)
97	Развёртка стены Г. Детская 2 (пом. 9)
98	Развёртки стен А, Б. Санузел (пом. 10)
99	Развёртки стен В, Г. Санузел (пом. 10)
100	Развёртка стены А. Гостиная (пом. 11)
101	Развёртка стены Б. Гостиная (пом. 11)
102	Развёртки стен В, Г. Гостиная (пом. 11)
103	Развёртки стен Б, В. Гардеробная 1 (пом. 12)
104	Развёртка стены Г. Гардеробная 1 (пом. 12)
105	Развёртки стен А, Б. Балкон 1 (пом. 13)
106	Развёртки стен В, Г. Балкон 1 (пом. 13)
107	Открытые вопросы, принятые допущения и конфликты. Лист 1 из 6
108	Открытые вопросы, принятые допущения и конфликты. Лист 2 из 6
109	Открытые вопросы, принятые допущения и конфликты. Лист 3 из 6
110	Открытые вопросы, принятые допущения и конфликты. Лист 4 из 6
111	Открытые вопросы, принятые допущения и конфликты. Лист 5 из 6
112	Открытые вопросы, принятые допущения и конфликты. Лист 6 из 6
Д1	Система хранения М-07
Д2	Система хранения М-08
Д3	Система хранения М-09
Д4	Шкаф распашной М-15
Д5	Система хранения М-17
Д6	Система хранения М-18
Д7	Шкаф-купе М-30
Д8	Система хранения М-33
Д9	Система хранения М-34
Д10	Шкаф распашной М-36
Д11	Система хранения М-40
Д12	Система хранения М-41
Д13	Система хранения М-42
Д14	Кухня (пом. 6). Развёртка гарнитура
Д15	Кухня (пом. 6). Развёртка гарнитура
Д16	Остров М-26 (пом. 6). Чертёж изделия
С1	Ведомость отделки помещений. Лист 1 из 2
С2	Ведомость отделки помещений. Лист 2 из 2
С3	Спецификация отделочных материалов
С4	Спецификация отделочных материалов
С5	Список покупок
С6	Список покупок (окончание)
С7	Смета проекта: этапы, помещения, итог
С8	Смета проекта: этапы, помещения, итог (продолжение)
С9	Смета проекта: этапы, помещения, итог (окончание)
С10	Смета материалов с ценами
С11	Смета материалов с ценами (продолжение)
С12	Смета материалов с ценами (продолжение)
С13	Смета материалов с ценами (окончание)
С14	Узлы
С15	Календарный график работ и закупок
С16	Чек-лист приёмки по этапам. Лист 1 из 3
С17	Чек-лист приёмки по этапам. Лист 2 из 3
С18	Чек-лист приёмки по этапам. Лист 3 из 3
С19	Лист → мастер

Общие указания

1. Размеры даны в мм от чистовых поверхностей стен: слой штукатурки 20 мм по блоку и 5 мм шпаклёвки по ГКЛ учтён. Перед заказом встроенной мебели — контрольный обмер после штукатурки.
2. Привязки мебели — от стен и углов помещения, а не от другой мебели.
3. Розетки, выводы и выключатели под мебель — см. лист 60 «План розеток и электровыводов»; сантехприборы и выводы воды — лист 39.
4. План расстановки не является документацией для изготовления мебели: изделия — по чертежам мебельщика; покупную мебель заменять только на изделия не больше габарита из спецификации (лист 33).
5. Встроенная мебель «стена в стену» — с зазором 10 мм с каждой стороны или с компенсаторами.
6. Развёртки — вид на стену изнутри помещения, по часовой стрелке; расположение стен на схеме листа развёртки; размеры — в мм по чистовым поверхностям; отметки — в м от ±0,000; высоты Н — от чистого пола помещения до оси изделия, у декора — до центра.
7. Красная цепочка — привязки электроточек и выводов по осям от угла чистовых стен; высота Н — у знака, от чистого пола до оси; высоты мебели, проёмов и границ отделки колонкой отметок слева. У знака — короткая марка; назначение, группа щита, высота и привязка каждой точки и вывода — в «Ведомости точек и выводов» под видами (каждая точка — строка).
8. У знака электроточки: марка (Р — розетка, S — выключатель, Св — светильник, ЭВ вывод кабеля), ×N — число постов в рамке, гр. — группа щита, Н — высота оси от чистого пола, мм; группы по клавишам выключателя — на листе выключателей.
9. Схема мебели, приборов и декора не является технической документацией для производства мебели; габариты — по паспортам изделий.
10. Марки позиций: М-NN — мебель, ОБ-NN — оборудование, С-NN — сантехника; О-N отделка (ведомость отделочных материалов, серия С).
11. Размеры мебели и изделий на заказ уточнить по месту после отделочных работ.

	Лист	№ док.	Подпись	Дата
Дизайнер	Кырлан А.С.			14.11.26
Проверил				
Н. контр.				
Утв.				

Проект: Четырёхкомнатная квартира

Список листов	Стадия	Лист	Листов
	П	20	147

выпуск 14.11.2026 № e7147312ff · стр. 20 из 147

Что в альбоме

Альбом — дизайн-проект с рабочими чертежами для ремонта. Листы идут в порядке работ: титул и вводные, реестр открытых вопросов и решений, планы (обмер, монтаж стен, мебель, двери, потолки, полы), инженерия (сантехника, электрика, вентиляция и отопление), развёртки стен с визуализациями помещений, чертежи мебели, ведомости материалов и узлы.

Вам как заказчику — титул, эта вводная, «Ваш проект на одной странице», реестр вопросов, план мебели, визуализации и развёртки, ведомости мебели и материалов. Подрядчику — всё остальное: монтажные планы, привязки выводов и розеток, узлы, ведомости объёмов.

Знаки на листах

Без знака — решение утверждено или подтверждено обмером.

Что проверить до ремонта

1. Розетки у кровати и рабочего места: хватает ли их с каждой стороны кровати и над столом (план розеток — лист 60).

2. Выводы под технику — варочная панель, духовка, посудомойка, стиральная машина, бойлер: совпадают ли с выбранными моделями (листы 33, 34, 35, 36, 37, 60).

3. Высоты розеток, выключателей и выводов даны от чистого пола: если мебель или техника будут другими — скажите до штробления стен.

Номера записей

К-N — открытый вопрос: чего не хватает или что выбрать (варианты и рекомендация — в тексте). Пока ответа нет, действует строка «если решения нет».

Кф-N — конфликт между разделами (например, мебель и радиатор в одном месте); закрывается решением, которое записывается как ИЗ-N.

ИЗ-N — изменение проекта: что было, что стало и кто утвердил. Изменение без подписи предложение.

Все записи — на листе реестра сразу после вводных; на других листах на них стоят ссылки.

Почему альбом предварительный

Обмера на объекте не было: размеры взяты с плана заказчика. Технические условия (мощность, вода, вентиляция дома) не получены, часть решений ждёт вашего ответа. Пока в реестре есть открытые вопросы, альбом предварительный — пометка в штампе снимается закрытием вопросов, а не стиранием.

Правку к любому листу можно оставить по кнопке «Правка к листу» или на сайте студии: дизайн-студия-квартир.рф — укажите номер листа и что изменить.

3 круга правок входят в цену; условия — в договоре и на странице вашего заказа на сайте студии.


Шифр проекта ГД-2026-004-АИ

	Лист	№ док.	Подпись	Дата	Проект: Четырёхкомнатная квартира			
Дизайнер	Кырлан А.С.			14.11.26	Как читать альбом	Стадия	Лист	Листов
Проверил						П	21	147
Н. контр.								
Утв.								

выпуск 14.11.2026 № e7147312ff · стр. 21 из 147

Отметки по высоте

±0,000	чистый пол пом. 1, 3–9, 11, 12; отсчёт высот
−0,015	чистый пол пом. 2, 10, ниже на 15 мм
−0,030	чистый пол пом. 13, ниже на 30 мм
−0,170	верх плиты — расчёт, не замер (задание на обмер)
сущ. пол	снимается до плиты; не замерен (задание на обмер)

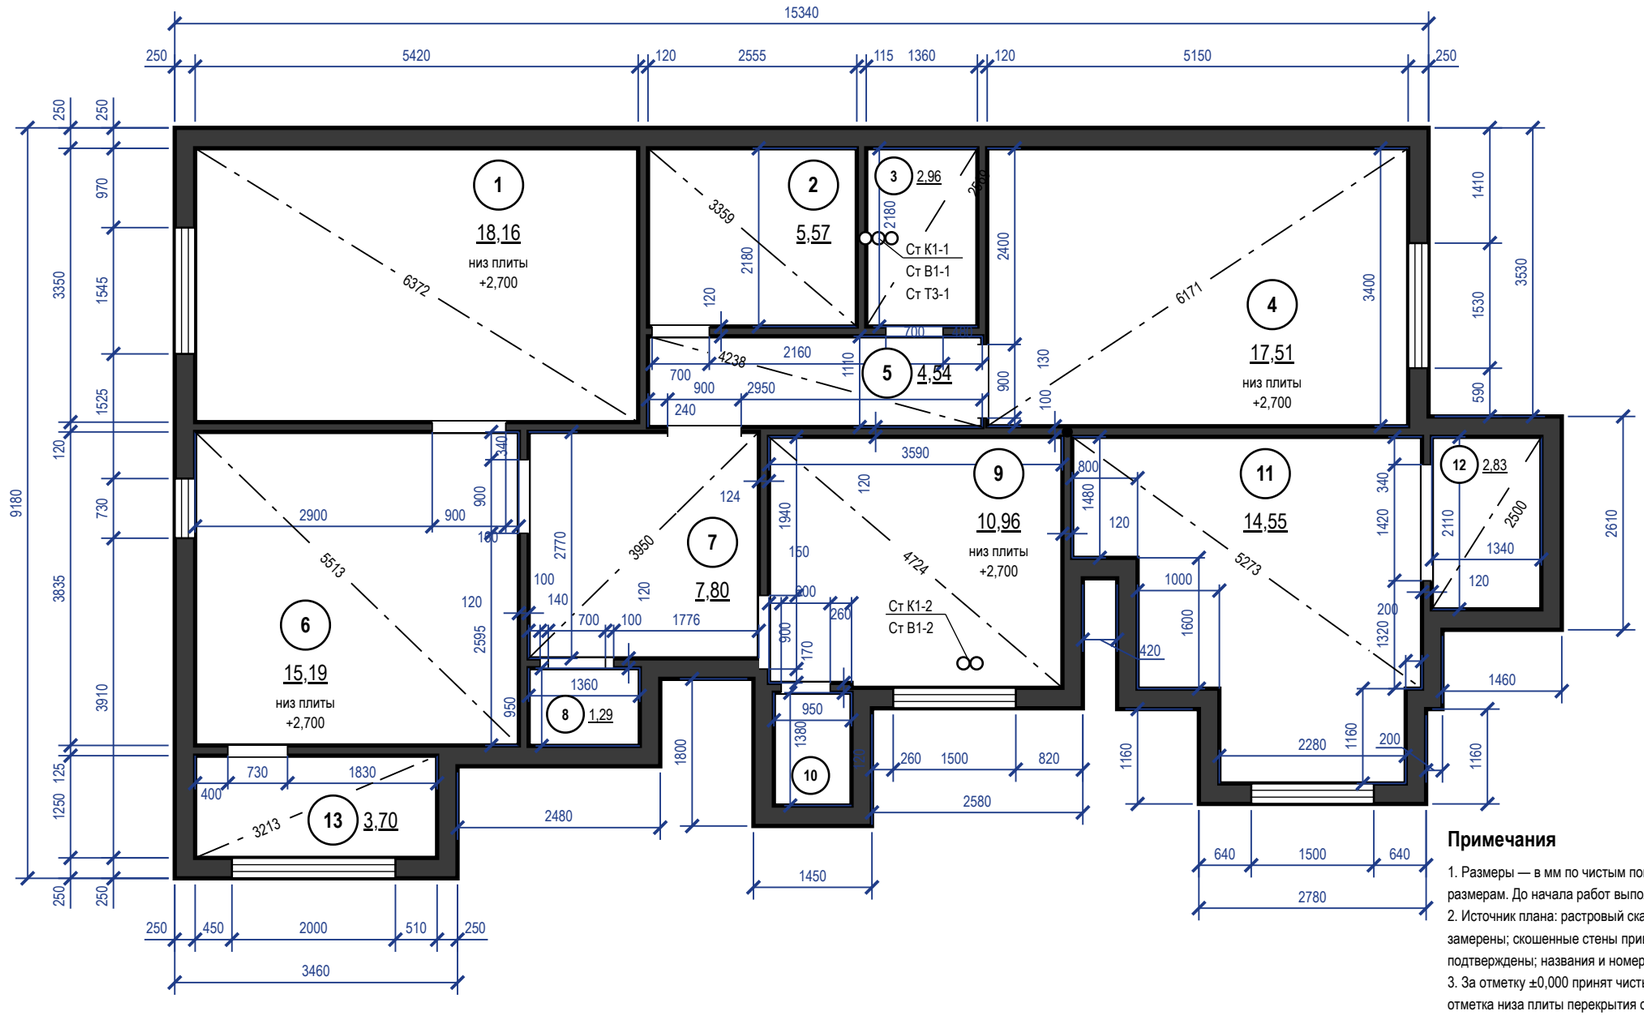

Экспликация помещений

№	Наименование	Площадь, м²
1	Зал	18,16
2	Ванная комната	5,57
3	Тёмная комната	2,96
4	Детская 1	17,51
5	Коридор	4,54
6	Кухня	15,19
7	Прихожая-коридор	7,80
8	Гардеробная 2	1,29
9	Детская 2	10,96
10	Санузел	1,31
11	Гостиная	14,55
12	Гардеробная 1	2,83
13	Балкон 1 *	3,70
	Итого (общая площадь)	**102,67**

Условные обозначения


- существующие стены (сечение)
- окно (рама, остекление)
- проём существующий, без заполнения (откосы)
- стояк: К1 — канализация, В1 — ХВС, Т3 — ГВС
- диагональ помещения — контроль прямоугольности
- (1) номер помещения, площадь м²

Примечания

1. Размеры — в мм по чистым поверхностям стен до отделки (по плану заказчика); площади — в м² по тем же размерам. До начала работ выполнить контрольный обмер.
2. Источник плана: растровый скан плана заказчика, размеры сняты с размерных цепочек, на объекте не замерены; скошенные стены приведены к ступеням (на плане не натура), углы 90° и диагонали не подтверждены; названия и номера помещений со сканом не сверены.
3. За отметку ±0,000 принят чистый пол, не существующий (блок отметок). «Низ плиты» у марки помещения отметка низа плиты перекрытия от ±0,000, как на развёртках и плане потолков (не высота потолка: потолок по плану потолков).
4. Толщины стен: наружные 250 мм, перегородки 120 мм; отличающиеся толщины и уступы — размерами на плане.
5. Несущие стены не определены: до технического заключения все стены считать несущими; проёмы и штробы в них не выполнять.
6. Дверные проёмы показаны без заполнения (двери — лист 50); высота дверных проёмов 2100 мм; низ окон (подоконник) 800, 900 мм от чистого пола, высота окон 1600, 1700 мм.
7. Диагонали — контрольные размеры; расхождение более 5 мм подписать на плане как перекос.
8. Размеры проверить на месте до начала работ; расхождение контрольных промеров ≤ 2 %.
9. Помещения, отмеченные *, в общую площадь квартиры и в итоги не входят.
10. Размеры короче 1 мм на листе цепочкой не показаны (две выносные линии на таком расстоянии сливаются): пом. 5, стена А — 50 мм от угла до проёма.

	Лист	№ док.	Подпись	Дата	Проект: Четырёхкомнатная квартира			М 1:75
Дизайнер	Кырлан А.С.			14.11.26	План планировки от заказчика	Стадия	Лист	Листов
Проверил						П	22	147
Н. контр.								
Утв.								

выпуск 14.11.2026 № e7147312ff · стр. 22 из 147

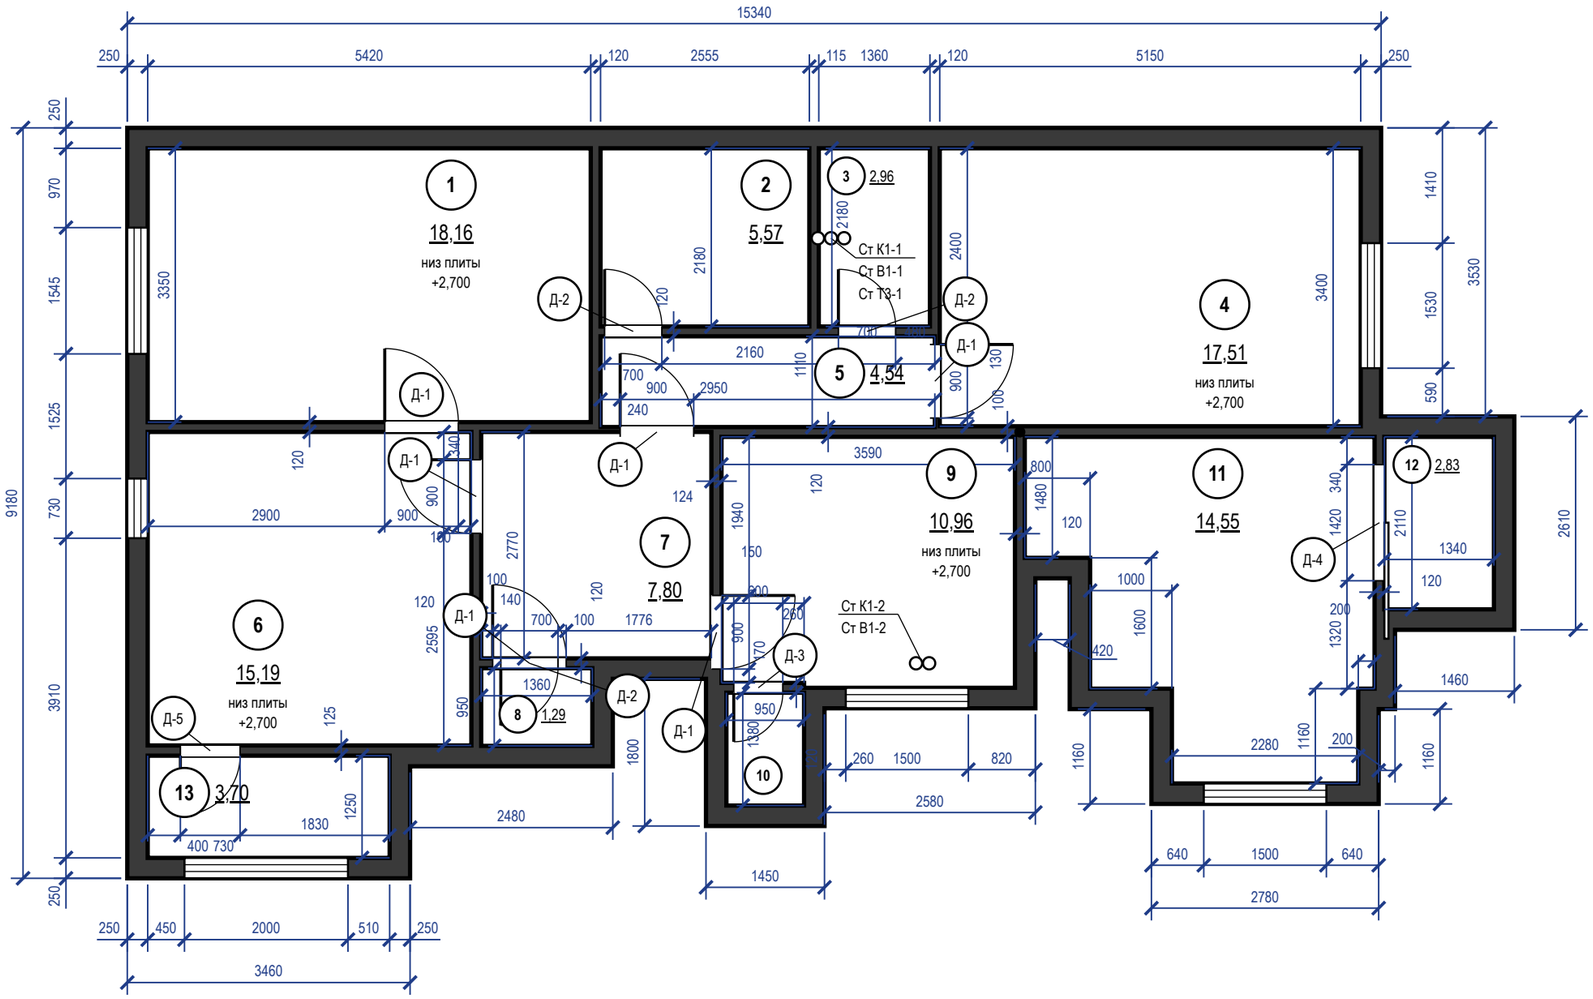

Экспликация помещений

№	Наименование	Площадь, м²
1	Зал	18,16
2	Ванная комната	5,57
3	Тёмная комната	2,96
4	Детская 1	17,51
5	Коридор	4,54
6	Кухня	15,19
7	Прихожая-коридор	7,80
8	Гардеробная 2	1,29
9	Детская 2	10,96
10	Санузел	1,31
11	Гостиная	14,55
12	Гардеробная 1	2,83
13	Балкон 1 *	3,70
	Итого (общая площадь)	**102,67**

Таблица проёмов

Марка	Наименование	Проём ш×в, мм	Полотно (расч.)
Д-1	Дверь распашная	900×2100	800×2000
Д-2	Дверь распашная	700×2100	600×2000
Д-3	Дверь распашная	600×2100	не задано (записи реестра нет)
Д-4	Дверь раздвижная	1420×2100	не задано (записи реестра нет)
Д-5	Дверь распашная	730×2100	не задано (записи реестра нет)

Примечания

1. Размеры — в мм от чистовых поверхностей стен до отделки; размеры уточнить по месту до начала работ.
2. Д-N, ПР-N в кружке — марка проёма: проём и полотно — по таблице проёмов, «расч.» полотно по проёму, заказ — по выбранной модели; ведомость, отделка и фурнитура — лист 50.
3. Несущие стены не изменять: проёмы, ниши и штробы в них — только по техническому заключению.
4. «расч.» — полотно, выведенное из проёма по запасу каталогов; заказ — по таблице проёмов выбранной модели; Д-1, Д-2: проём 2100, а под полотно 2000 по каталогам нужен 2040–2080, под 2100 — 2140–2180: высоту проёма — по модели; Д-3: проём 600×2100 вне ряда стандартных полотен — полотно задать при выборе модели; Д-4: раздвижная, полотно — по системе — полотно задать при выборе модели; Д-5: проём 730×2100 вне ряда стандартных полотен — полотно задать при выборе модели.
5. Размеры короче 1 мм на листе цепочкой не показаны (две выносные линии на таком расстоянии сливаются): пом. 5, стена А — 50 мм от угла до проёма.

	Лист	№ док.	Подпись	Дата
Дизайнер	Кырлан А.С.			14.11.26
Проверил				
Н. контр.				
Утв.				


Проект: Четырёхкомнатная квартира — **М 1:75**

План монтажный


Стадия	Лист	Листов
П	23	147

выпуск 14.11.2026 № e7147312ff · стр. 23 из 147

Привязка выводов и крепление модулей (М 1:20)

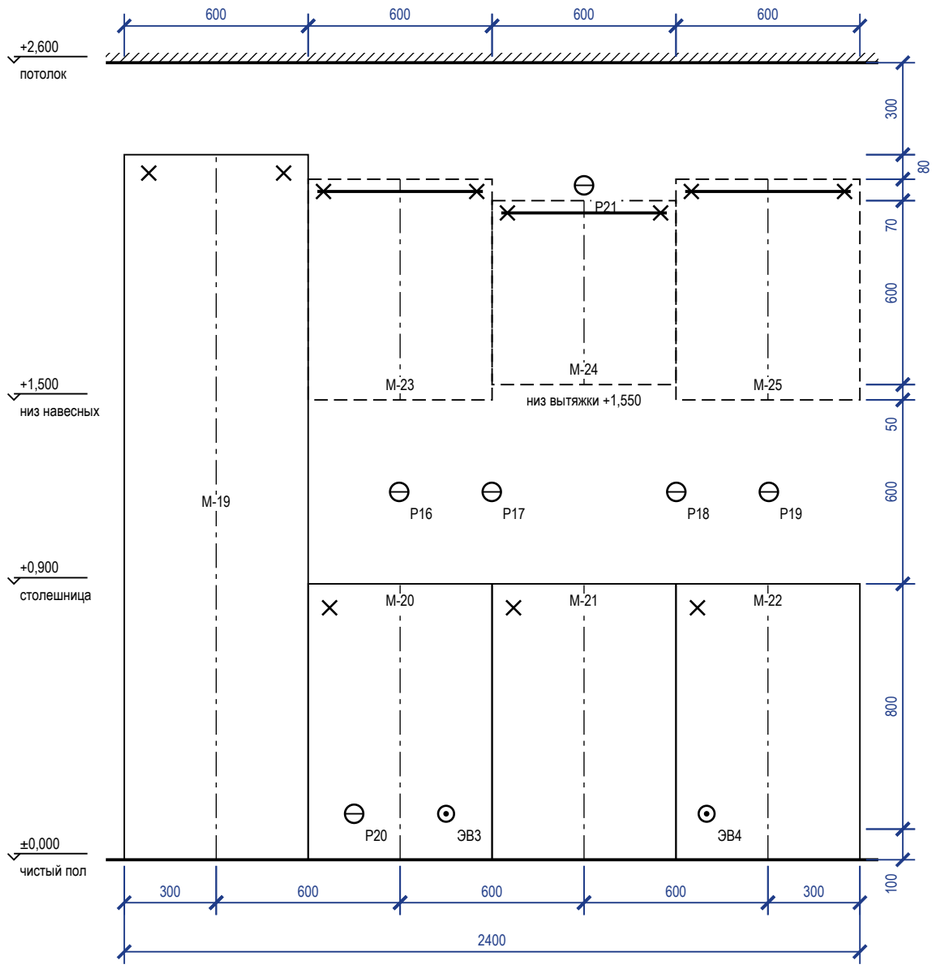

План столешницы (М 1:20)

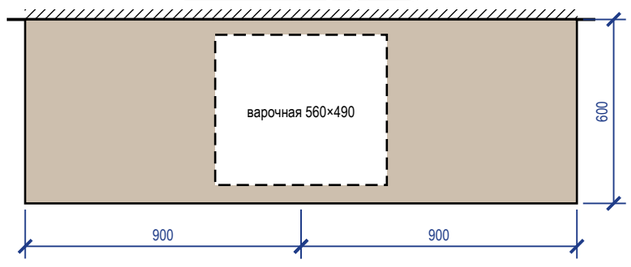

Привязка выводов к осям модулей

Код	Назначение	Модуль	От оси, мм	H, мм	Размещение
P20	розетка — холодильник встроенный M-19 (розетка в модуле M-20)	M-20	−150	150	в соседнем модуле, за ящиком
P16	розетка ×2 — фартук: мелкая техника	M-20	−3	1200	над столешницей (фартук)
ЭВ3	вывод кабеля — варочная панель M-21	M-20	+150	150	в соседнем модуле, за ящиком
P17	розетка ×2 — фартук: мелкая техника	M-20	+299	1200	над столешницей (фартук)
P21	розетка — вытяжка M-24 (в модуле, съёмная панель)	M-24	0	2200	в навесном модуле
P18	розетка ×2 — фартук: мелкая техника	M-21	+301	1200	над столешницей (фартук)
ЭВ4	вывод кабеля — духовой шкаф M-21 (вывод в соседнем модуле M-22)	M-22	−200	150	в соседнем модуле, за ящиком
P19	розетка ×2 — фартук: мелкая техника	M-22	+3	1200	над столешницей (фартук)

Зазоры под отделку

Поверхность	Отделка	Зазор, мм	Учесть
фартук	керамогранит	10	от чернового основания до корпуса навесных и столешницы
стены	окраска	5	под штукатурку и шпаклёвку за пеналом
пол	инженерная доска		цоколь — после укладки пола, опоры ±20 мм

Условные обозначения


- нижний модуль, пенал (контур)
- невидимый контур: навесной модуль, корпус под столешницей
- ось модуля (от неё — привязка вывода)
- анкер / уголок крепления к стене
- розетка на стене
- вывод кабеля к технике
- B1 — вывод воды B1 / Т3, канализации К1

Примечания

1. Выводы — по проекту электрики и ВК; привязка по горизонтали — от оси модуля (плюс — вправо по виду), по высоте — от чистого пола до оси вывода.
2. Пенал — уголки к стене 2 шт. сверху; нижние модули — стяжками между собой и уголком к стене; ряд выставить по уровню опорами цоколя.
3. Розетки над столешницей — не ниже 150 мм над ней и не за корпусом техники; розетка за ПММ, духовым шкафом и холодильником — только в соседнем модуле или в зоне цоколя с доступом.
4. Столешница — вырезы по шаблонам выбранных моделей мойки и варочной панели; торцы у стены — герметик, пристеночный плинтус.

	Лист	№ док.	Подпись	Дата	Проект: Четырёхкомнатная квартира	М 1:20		
Дизайнер	Кырлан А.С.			14.11.26	Кухня (пом. 6). Монтажная схема	Стадия	Лист	Листов
Проверил						П	24	147
Н. контр.								
Утв.								

Привязка выводов и крепление модулей (М 1:20)

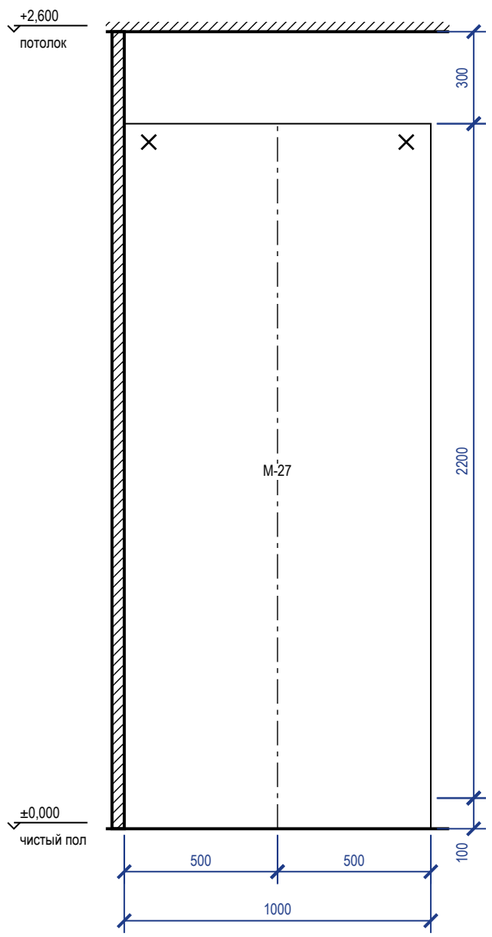

Привязка выводов к осям модулей

Код	Назначение	Модуль	От оси, мм	Н, мм	Размещение

Зазоры под отделку

Поверхность	Отделка	Зазор, мм	Учесть
фартук	керамогранит	10	от чернового основания до корпуса навесных и столешницы
стены	окраска	5	под штукатурку и шпаклёвку за пеналом
пол	инженерная доска		цоколь — после укладки пола, опоры ±20 мм

Условные обозначения


- нижний модуль, пенал (контур)
- ось модуля (от неё — привязка вывода)
- анкер / уголок крепления к стене
- розетка на стене
- вывод кабеля к технике
- B1 — вывод воды В1 / Т3, канализации К1

Примечания


1. Выводы — по проекту электрики и ВК; привязка по горизонтали — от оси модуля (плюс — вправо по виду), по высоте — от чистого пола до оси вывода.
2. Пенал — уголки к стене 2 шт. сверху; нижние модули — стяжками между собой и уголком к стене; ряд выставить по уровню опорами цоколя.
3. Розетки над столешницей — не ниже 150 мм над ней и не за корпусом техники; розетка за ПММ, духовым шкафом и холодильником — только в соседнем модуле или в зоне цоколя с доступом.
4. Столешница — вырезы по шаблонам выбранных моделей мойки и варочной панели; торцы у стены — герметик, пристеночный плинтус.

	Лист	№ док.	Подпись	Дата	Проект: Четырёхкомнатная квартира		М 1:20	
Дизайнер	Кырлан А.С.			14.11.26	Кухня (пом. 6). Монтажная схема	Стадия	Лист	Листов
Проверил						П	25	147
Н. контр.								
Утв.								


М-07 (пом. 2) (М 1:40)

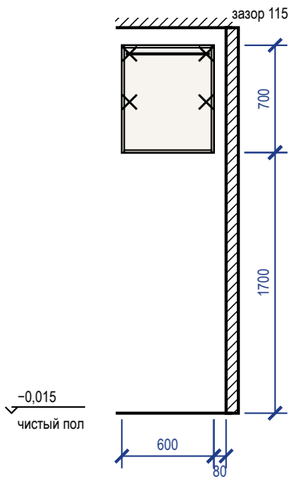


Система хранения М-08 (пом. 3) (М 1:40)

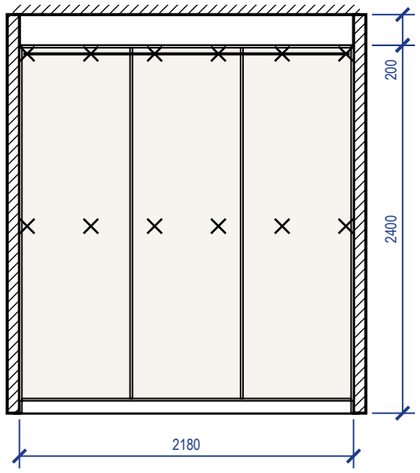


Система хранения М-09 (пом. 3) (М 1:40)

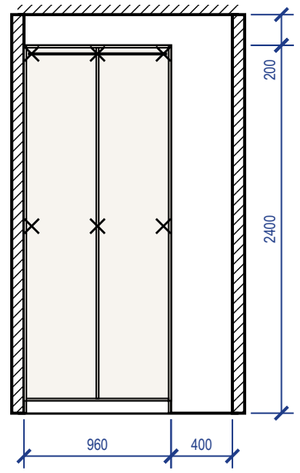

Шкаф распашной М-15 (пом. 4) (М 1:40)

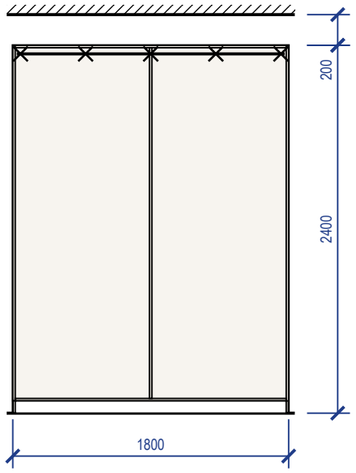

Система хранения М-17 (пом. 4) (М 1:40)

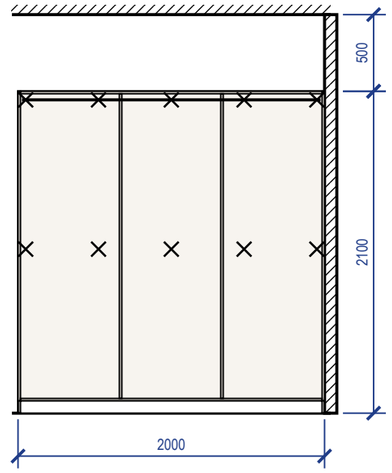

Крепление и зазоры под отделку (изделия листа 1)

Марка	Помещение, стена	Основание	Отделка стены	Зазор, мм	Крепёж по планке	От опрокидывания
М-07	Ванная комната (2), стена Б	по основанию — см. таблицу крепежа	плитка	10	анкер 4 шт. (2 ряда)	крепление к стене, 2 точки
М-08	Тёмная комната (3), стена Б	по основанию — см. таблицу крепежа	окраска	5	анкер 12 шт. (2 ряда)	крепление к стене, 4 точки
М-09	Тёмная комната (3), стена А	по основанию — см. таблицу крепежа	окраска	5	анкер 6 шт. (2 ряда)	крепление к стене, 3 точки
М-15	Детская 1 (4), стена В	по основанию — см. таблицу крепежа	окраска	5	анкер 5 шт., шаг 425	уголок к стене, 3 шт.
М-17	Детская 1 (4), стена Г	по основанию — см. таблицу крепежа	окраска	5	анкер 10 шт. (2 ряда)	крепление к стене, 3 точки

Крепёж по основанию стены

Основание стены	Крепёж
бетон, ж/б	анкер-шуруп 7,5×72 или дюбель 8×60 с шурупом 5×70
кирпич полнотелый	дюбель 8×80 с шурупом 5×90
газобетон, пазогребень	дюбель для газобетона 10×100 или химический анкер
гипсокартон	закладная до обшивки (брус 40×80 или фанера 18 мм), саморез в закладную

Условные обозначения

- анкер / уголок крепления к стене
- корпус и полки ЛДСП (вид на стену)
- компенсатор — короб до потолка


Примечания

1. Установочные размеры — от чистого пола и чистых стен; перед установкой контрольный замер после отделки.
2. Порядок: корпус выставить по уровню опорами цоколя → закрепить к стене по задней планке → навесить двери и фасады, отрегулировать зазоры → подогнать и закрепить компенсатор.
3. Анкеры — с шагом не более 500 мм, не ближе 50 мм от края планки; на ГКЛ только в закладную, установленную до обшивки.
4. Скрытые коммуникации под анкеры проверить детектором; трассы электрики по плану розеток.
5. Монтажная схема на 3 листах, лист 1 из 3; продолжение — на следующем листе схемы. Условные обозначения, таблица крепежа по основанию и примечания повторены на каждом листе.


	Лист	№ док.	Подпись	Дата	Проект: Четырёхкомнатная квартира		М 1:40	
Дизайнер	Кырлан А.С.			14.11.26	Шкафы. Монтажная схема. Лист 1 из 3	Стадия	Лист	Листов
Проверил						П	26	147
Н. контр.								
Утв.								

выпуск 14.11.2026 № e7147312ff · стр. 26 из 147


Система хранения М-18 (пом. 5) (М 1:40)

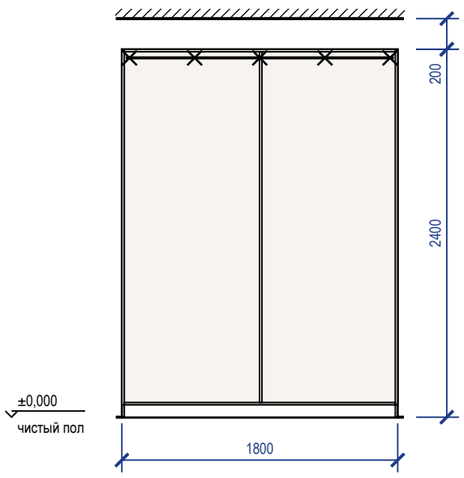


Шкаф-купе М-30 (пом. 7) (М 1:40)

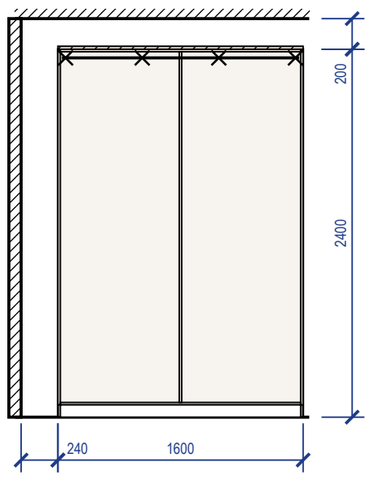


Система хранения М-33 пом. 8 (М 1:40)

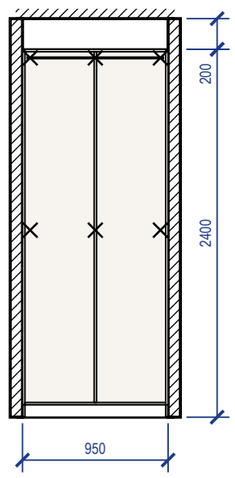

Система хранения М-34 (пом. 8) (М 1:40)

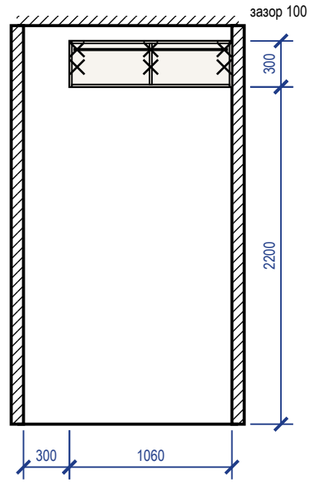

Шкаф распашной М-36 (пом. 9) (М 1:40)

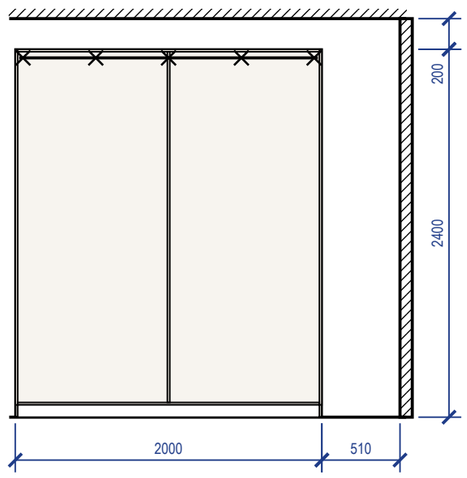

Крепление и зазоры под отделку (изделия листа 2)

Марка	Помещение, стена	Основание	Отделка стены	Зазор, мм	Крепёж по планке	От опрокидывания
М-18	Коридор (5), стена А	по основанию — см. таблицу крепежа	окраска	5	анкер 5 шт., шаг 425	крепление к стене, 4 точки
М-30	Прихожая-коридор (7), стена Б	по основанию — см. таблицу крепежа	окраска	5	анкер 4 шт., шаг 500	крепление к стене, 3 точки
М-33	Гардеробная 2 (8), стена Б	по основанию — см. таблицу крепежа	окраска	5	анкер 6 шт. (2 ряда)	крепление к стене, 3 точки
М-34	Гардеробная 2 (8), стена В	по основанию — см. таблицу крепежа	окраска	5	анкер 6 шт. (2 ряда)	крепление к стене, 4 точки
М-36	Детская 2 (9), стена А	по основанию — см. таблицу крепежа	окраска	5	анкер 5 шт., шаг 475	уголок к стене, 3 шт.

Крепёж по основанию стены

Основание стены	Крепёж
бетон, ж/б	анкер-шуруп 7,5×72 или дюбель 8×60 с шурупом 5×70
кирпич полнотелый	дюбель 8×80 с шурупом 5×90
газобетон, пазогребень	дюбель для газобетона 10×100 или химический анкер
гипсокартон	закладная до обшивки (брус 40×80 или фанера 18 мм), саморез в закладную

Условные обозначения

- анкер / уголок крепления к стене
- корпус и полки ЛДСП (вид на стену)
- компенсатор — короб до потолка


Примечания

1. Установочные размеры — от чистого пола и чистых стен; перед установкой контрольный замер после отделки.
2. Порядок: корпус выставить по уровню опорами цоколя → закрепить к стене по задней планке → навесить двери и фасады, отрегулировать зазоры → подогнать и закрепить компенсатор.
3. Анкеры — с шагом не более 500 мм, не ближе 50 мм от края планки; на ГКЛ только в закладную, установленную до обшивки.
4. Скрытые коммуникации под анкеры проверить детектором; трассы электрики по плану розеток.
5. Монтажная схема на 3 листах, лист 2 из 3; продолжение — на следующем листе схемы. Условные обозначения, таблица крепежа по основанию и примечания повторены на каждом листе.


	Лист	№ док.	Подпись	Дата	Проект: Четырёхкомнатная квартира			М 1:40
Дизайнер	Кырлан А.С.			14.11.26	Шкафы. Монтажная схема. Лист 2 из 3	Стадия	Лист	Листов
Проверил						П	27	147
Н. контр.								
Утв.								

выпуск 14.11.2026 № e7147312ff · стр. 27 из 147


Система хранения М-40 (пом. 12) (М 1:40)

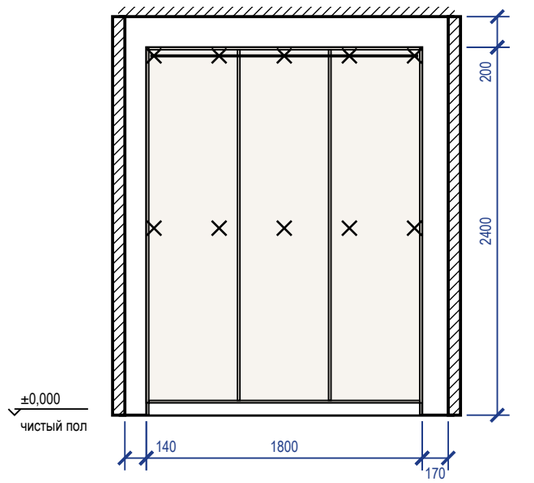

Система хранения М-41 пом. 13 (М 1:40)

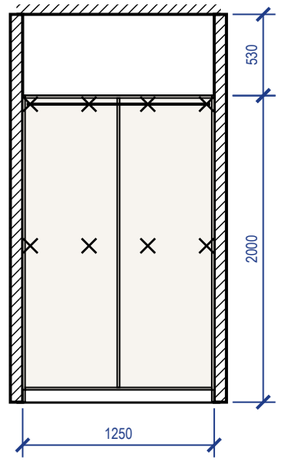

Система хранения М-42 пом. 13 (М 1:40)

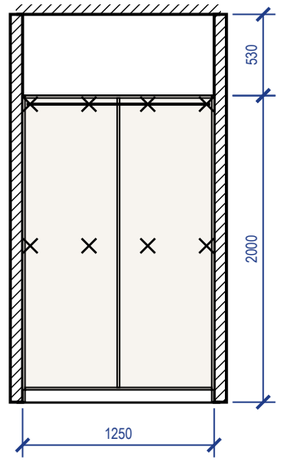

Крепление и зазоры под отделку (изделия листа 3)

Марка	Помещение, стена	Основание	Отделка стены	Зазор, мм	Крепёж по планке	От опрокидывания
М-40	Гардеробная 1 (12), стена Б	по основанию — см. таблицу крепежа	окраска	5	анкер 10 шт. (2 ряда)	крепление к стене, 4 точки
М-41	Балкон 1 (13), стена Б	по основанию — см. таблицу крепежа	окраска	5	анкер 8 шт. (2 ряда)	крепление к стене, 3 точки
М-42	Балкон 1 (13), стена Г	по основанию — см. таблицу крепежа	окраска	5	анкер 8 шт. (2 ряда)	крепление к стене, 3 точки

Крепёж по основанию стены

Основание стены	Крепёж
бетон, ж/б	анкер-шуруп 7,5×72 или дюбель 8×60 с шурупом 5×70
кирпич полнотелый	дюбель 8×80 с шурупом 5×90
газобетон, пазогребень	дюбель для газобетона 10×100 или химический анкер
гипсокартон	закладная до обшивки (брус 40×80 или фанера 18 мм), саморез в закладную

Условные обозначения


- анкер / уголок крепления к стене
- корпус и полки ЛДСП (вид на стену)
- компенсатор — короб до потолка

Примечания

1. Установочные размеры — от чистого пола и чистых стен; перед установкой контрольный замер после отделки.
2. Порядок: корпус выставить по уровню опорами цоколя → закрепить к стене по задней планке → навесить двери и фасады, отрегулировать зазоры → подогнать и закрепить компенсатор.
3. Анкеры — с шагом не более 500 мм, не ближе 50 мм от края планки; на ГКЛ только в закладную, установленную до обшивки.
4. Скрытые коммуникации под анкеры проверить детектором; трассы электрики по плану розеток.
5. Монтажная схема на 3 листах, лист 3 из 3. Условные обозначения, таблица крепежа по основанию и примечания повторены на каждом листе.

	Лист	№ док.	Подпись	Дата	Проект: Четырёхкомнатная квартира	М 1:40		
Дизайнер	Кырлан А.С.			14.11.26	Шкафы. Монтажная схема. Лист 3 из 3	Стадия	Лист	Листов
Проверил						П	28	147
Н. контр.								
Утв.								

выпуск 14.11.2026 № e7147312ff · стр. 28 из 147

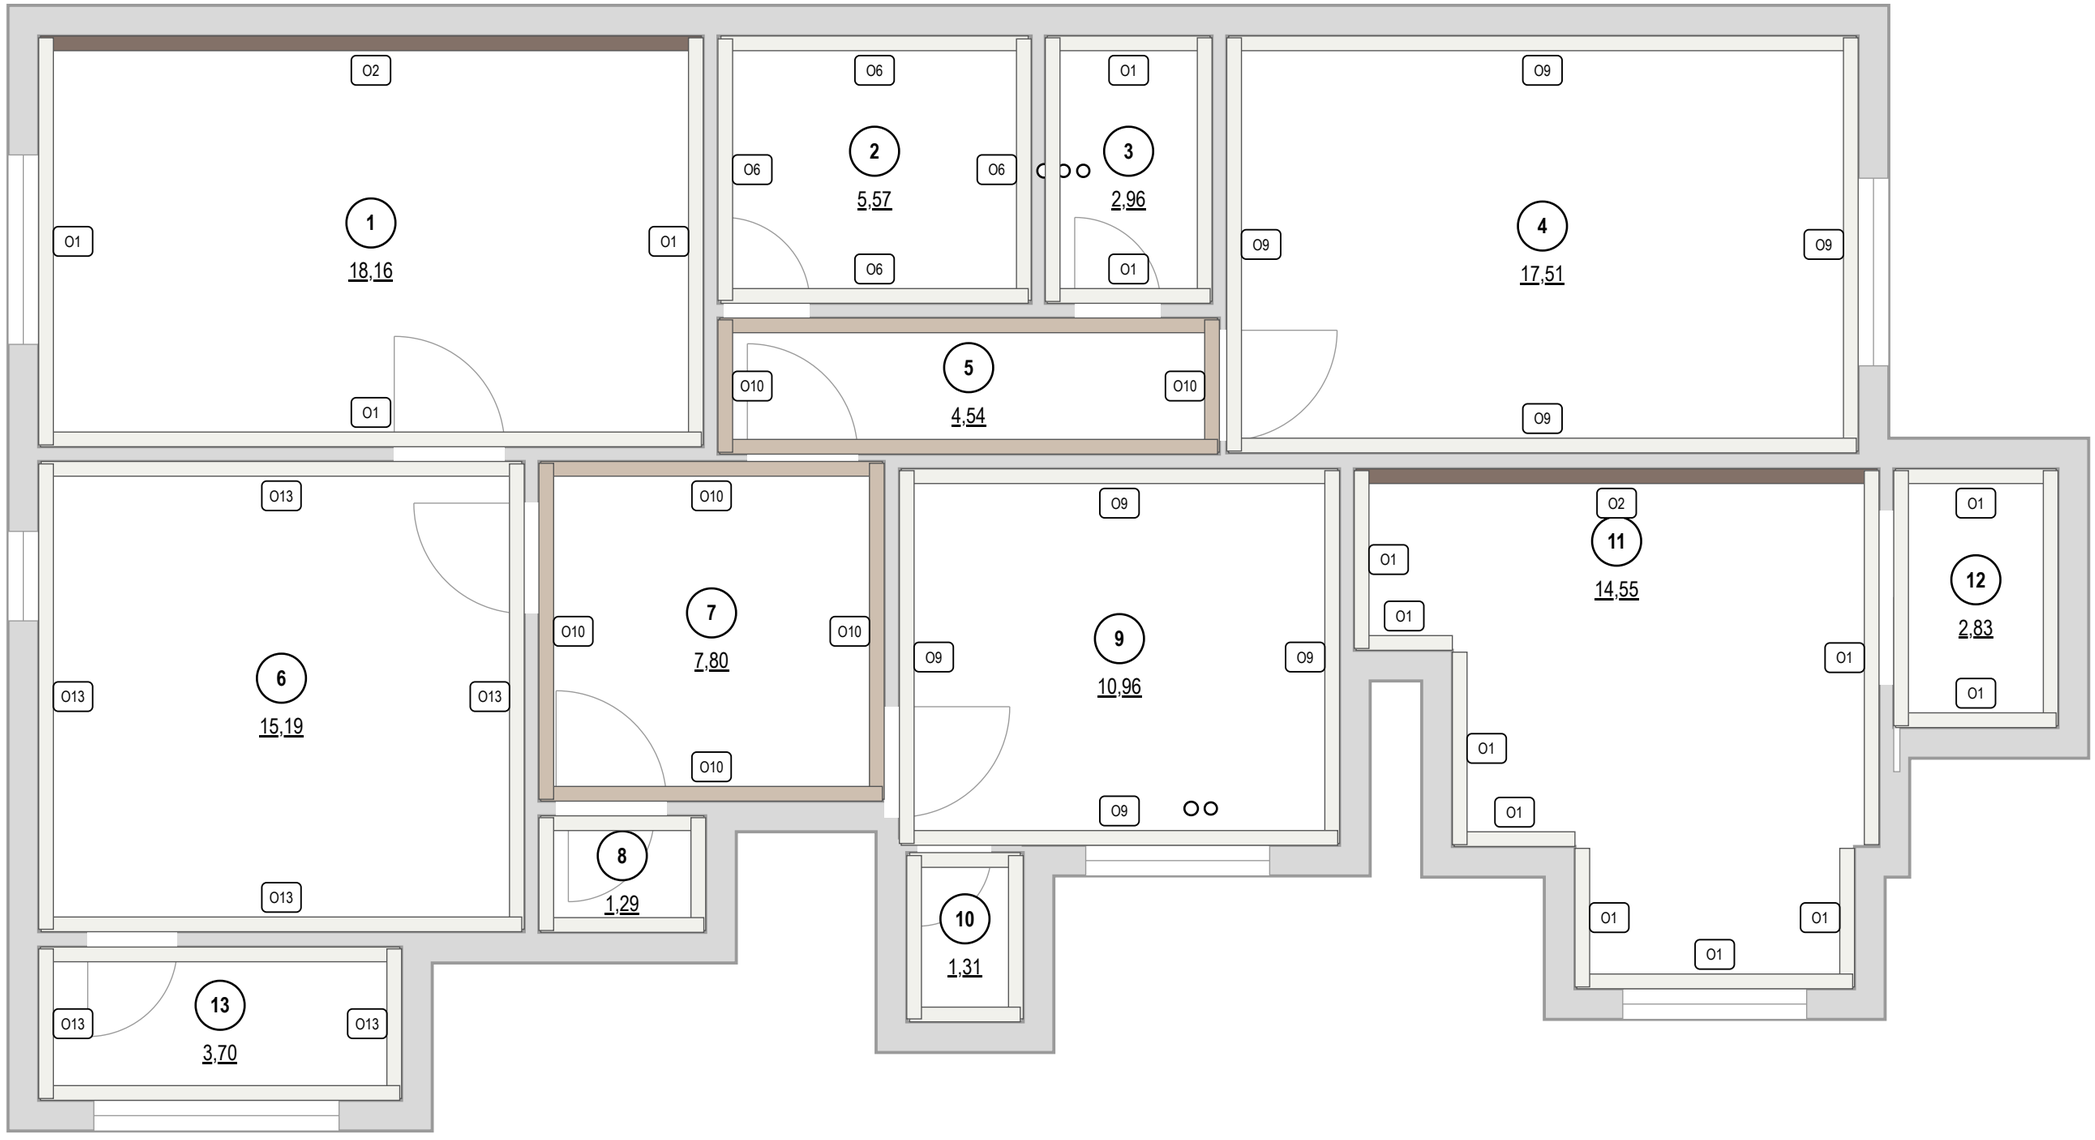

Покрытия стен

Марка	Покрытие	Помещение: S, м²	Итого, м²
O1	окраска Tikkurila · F497 «Paper»	1: 27,2; 3: 16,6; 8: 8,3; 11: 27,0; 12: 14,6	93,8
O2	окраска Tikkurila · L481 «Silhouette»	1: 13,5; 11: 11,1	24,5
O6	облицовка плиткой · «тон Paper F497» 600×600 мм	2: 21,9; 10: 10,0	31,8
O9	окраска Tikkurila · F497 «Paper»	4: 40,1; 9: 29,1	69,3
O10	окраска Tikkurila · J484 «Castle»	5: 20,0; 7: 20,0	40,0
O13	окраска Tikkurila · F497 «Paper»	6: 32,9; 13: 16,4	49,3

Площади — нетто, по развёрткам (за вычетом проёмов и фартука); высоты помещений — от чистого пола.

	Лист	№ док.	Подпись	Дата	Проект: Четырёхкомнатная квартира			M 1:50
Дизайнер	Кырлан А.С.			14.11.26				
Проверил					Карта покрытий стен	Стадия	Лист	Листов
Н. контр.						П	29	147
Утв.								

выпуск 14.11.2026 № e7147312ff · стр. 29 из 147

Колерная карта по помещениям

Помещение	Поверхность	Образец	Поз.	Система и код цвета	Производитель, линейка / материал, артикул	Блеск	Класс истирания	LRV	Площадь
1. Зал 18,16 м²	стены		**K1**	Tikkurila F497	Tikkurila · Optiva 5 Matt	матовая	2	88	25,9 м²
	акцент А		**K2**	Tikkurila L481	Tikkurila · Optiva 5 Matt	матовая	2	18	13,6 м²
	потолок		**K3**	Tikkurila F497	Tikkurila · Anti-Reflex 2	глубокомат.	2	88	18,2 м²
	пол		**KM1**	по образцу	инженерная доска · аналог по хар.				18,2 м²
	плинтус		**K4**	Tikkurila F497	МДФ · в цвет Tikkurila	полуглянц.	2	88	16,6 м
2. Ванная комната 5,57 м²	стены		**KM2**	тон Paper F497 (тёплый белый)	плитка · аналог по хар.				22,3 м²
	потолок		**K5**	Tikkurila F497	Tikkurila · Luja 7	матовая	1	88	5,6 м²
	пол		**KM3**	тон Castle J484 (тёплый песочный)	керамогранит · аналог по хар.				5,6 м²
3. Тёмная комната 2,96 м²	стены		**K1**	Tikkurila F497	Tikkurila · Optiva 5 Matt	матовая	2	88	16,9 м²
	потолок		**K3**	Tikkurila F497	Tikkurila · Anti-Reflex 2	глубокомат.	2	88	3,0 м²
	пол		**KM1**	по образцу	инженерная доска · аналог по хар.				3,0 м²
	плинтус		**K4**	Tikkurila F497	МДФ · в цвет Tikkurila	полуглянц.	2	88	6,4 м
4. Детская 1 17,51 м²	стены		**K6**	Tikkurila F497	Tikkurila · Joker	полуматов.	2	88	40,1 м²
	потолок		**K3**	Tikkurila F497	Tikkurila · Anti-Reflex 2	глубокомат.	2	88	17,5 м²
	пол		**KM1**	по образцу	инженерная доска · аналог по хар.				17,5 м²
	плинтус		**K4**	Tikkurila F497	МДФ · в цвет Tikkurila	полуглянц.	2	88	16,2 м
5. Коридор 4,54 м²	стены		**K7**	Tikkurila J484	Tikkurila · Optiva 20 Semimatt	полуматов.	2	55	22,2 м²
	потолок		**K3**	Tikkurila F497	Tikkurila · Anti-Reflex 2	глубокомат.	2	88	4,5 м²
	пол		**KM4**	тон Claystone V486 (грейж)	керамогранит · аналог по хар.				4,5 м²
	плинтус		**K8**	Tikkurila J484	МДФ · в цвет Tikkurila	полуглянц.	2	55	8,1 м
6. Кухня 15,19 м²	стены		**K9**	Tikkurila F497	Tikkurila · Luja 7	полуматов.	1	88	34,5 м²
	потолок		**K5**	Tikkurila F497	Tikkurila · Luja 7	матовая	1	88	15,2 м²
	пол		**KM1**	по образцу	инженерная доска · аналог по хар.				15,2 м²
	плинтус		**K4**	Tikkurila F497	МДФ · в цвет Tikkurila	полуглянц.	2	88	13,8 м
	фартук		**KM5**	тон Paper F497 (тёплый белый)	керамогранит · аналог по хар.				1,1 м²

Схема палитры проекта

Стиль: Современный (контемпорари) · схема: аналоговая

основной	основной	второстепенный	акцентный
Tikkurila F497	**Tikkurila J484**	**Tikkurila V486**	**Tikkurila L481**
Paper LRV 88 стены 1,3,4,6,8,9,11,12,13; потолок 1,2,3,4,5,6,7,8,9,10,11,12,13; плинтус 1,3,4,6,8,9,11,12; текстиль/декор 1,2	Castle LRV 55 стены 5,7; плинтус 5,7; текстиль/декор 1,6	Claystone LRV 44 текстиль/декор 1,2,13	Silhouette LRV 18 акцент 1,11; текстиль/декор 1,2,6,11

План 60/30/10

60%	30%	10%

Окраска, факт — по площади стен, акцентов, потолков

94%	6%

окрашено всего 391,5 м²; второстепенный тон несут мебель и текстиль

Текстиль и декор в цветах вне палитры проекта

- NCS S 3005-Y20R тёплый тауп-серый — пом. 1 (T3), 7 (T15), 9 (T18)
- Tikkurila H487 Pumice — пом. 1 (T4), 4 (T9, T10, T11), 9 (T17, T19)
- NCS S 5010-B10G серо-петроль — пом. 1 (ДК30), 4 (T12, T13), 7 (ДК25)
- Tikkurila V484 Driftwood — пом. 4 (T8), 9 (T16), 13 (T23)
- Farrow & Ball No. 47 Green Smoke — пом. 4 (ДК34), 9 (T20, T21), 10 (ДК24)

Условные обозначения

- **K1** Tikkurila F497 · Paper · Optiva 5 Matt · матовая · кл. 2
- **K2** Tikkurila L481 · Silhouette · Optiva 5 Matt · матовая · кл. 2
- **K3** Tikkurila F497 · Paper · Anti-Reflex 2 · глубокомат. · кл. 2
- **K4** Tikkurila F497 · Paper · МДФ · полуглянц. · кл. 2
- **K5** Tikkurila F497 · Paper · Luja 7 · матовая · кл. 1
- **K6** Tikkurila F497 · Paper · Joker · полуматов. · кл. 2
- **K7** Tikkurila J484 · Castle · Optiva 20 Semimatt · полуматов. · кл. 2
- **K8** Tikkurila J484 · Castle · МДФ · полуглянц. · кл. 2
- **K9** Tikkurila F497 · Paper · Luja 7 · полуматов. · кл. 1
- дерево (доска, паркет, ламинат) — рисунок досок
- керамогранит, плитка, камень — сетка швов по формату
- **KM1** инженерная доска · аналог: дуб натуральный брашированный, масло-воск, 14/4 мм
- **KM2** плитка · аналог: керамогранит матовый, тон F497, 600×600×9 мм
- **KM3** аналог: керамогранит матовый R10, тон J484, 600×600×10 мм
- **KM4** аналог: керамогранит матовый R10, тон V486, 600×600×10 мм
- **KM5** аналог: керамогранит матовый, тон F497, 600×600×9 мм
- **KM6** аналог: керамогранит матовый R11, тон V486, 600×600×10 мм
- **KM7** керамогранит · аналог: плинтус из керамогранита пола, подрезка 80 мм, верхняя кромка с запилом 45°

K — краска, KM — отделочный материал (тон KM — по описанию, эталон — образец материала); кл. — класс истирания (1 — самый стойкий к мытью);
LRV — светлота цвета: 0 — чёрный, 100 — белый

Примечания

1. Цвет на листе и на экране — ориентир. До покраски — выкрас на объекте: не меньше А3 (или лист ГКЛ), на грунте под эту краску, не на белой шпаклёвке, в 2 слоя; на обороте — код, бренд, веер, дата. Смотреть днём и вечером, рядом с образцами пола и плитки. Красить только в цвет утверждённого выкраса.
2. Краску заказывать по коду из графы «Система и код цвета» у бренда этого кода, не «аналогом» другого; весь объём одного кода — одной партией, колеруемую краску — за один проход машины.
3. Площади — те же, что в ведомости отделки (лист С1); сколько краски заказать — в спецификации отделочных материалов (лист С3).
4. Колерная карта на 2 листах: обозначения — на каждом, схема и палитра — на первом, выкрасы — на последнем.

	Лист	№ док.	Подпись	Дата	Проект: Четырёхкомнатная квартира			
Дизайнер	Кырлан А.С.			14.11.26	Колерная карта	Стадия	Лист	Листов
Проверил						П	30	147
Н. контр.								
Утв.								

выпуск 14.11.2026 № e7147312ff · стр. 30 из 147

Колерная карта по помещениям (продолжение)

Помещение	Поверхность	Образец	Поз.	Система и код цвета	Производитель, линейка / материал, артикул	Блеск	Класс истирания	LRV	Площадь
7. Прихожая-коридор 7,8 м²	стены		**К7**	Tikkurila J484	Tikkurila · Optiva 20 Semimatt	полуматов.	2	55	23,8 м²
	потолок		**К3**	Tikkurila F497	Tikkurila · Anti-Reflex 2	глубокомат.	2	88	7,8 м²
	пол		**КМ4**	тон Claystone V486 (грейж)	керамогранит · аналог по хар.				7,8 м²
	плинтус		**К8**	Tikkurila J484	МДФ · в цвет Tikkurila	полуглянц.	2	55	8,7 м
8. Гардеробная 2 1,29 м²	стены		**К1**	Tikkurila F497	Tikkurila · Optiva 5 Matt	матовая	2	88	8,7 м²
	потолок		**К3**	Tikkurila F497	Tikkurila · Anti-Reflex 2	глубокомат.	2	88	1,3 м²
	пол		**КМ1**	по образцу	инженерная доска · аналог по хар.				1,3 м²
	плинтус		**К4**	Tikkurila F497	МДФ · в цвет Tikkurila	полуглянц.	2	88	3,3 м
9. Детская 2 10,96 м²	стены		**К6**	Tikkurila F497	Tikkurila · Joker	полуматов.	2	88	29,1 м²
	потолок		**К3**	Tikkurila F497	Tikkurila · Anti-Reflex 2	глубокомат.	2	88	11,0 м²
	пол		**КМ1**	по образцу	инженерная доска · аналог по хар.				11,0 м²
	плинтус		**К4**	Tikkurila F497	МДФ · в цвет Tikkurila	полуглянц.	2	88	11,8 м
10. Санузел 1,31 м²	стены		**КМ2**	тон Paper F497 (тёплый белый)	плитка · аналог по хар.				10,5 м²
	потолок		**К5**	Tikkurila F497	Tikkurila · Luja 7	матовая	1	88	1,3 м²
	пол		**КМ3**	тон Castle J484 (тёплый песочный)	керамогранит · аналог по хар.				1,3 м²
11. Гостиная 14,55 м²	стены		**К1**	Tikkurila F497	Tikkurila · Optiva 5 Matt	матовая	2	88	27,8 м²
	акцент А		**К2**	Tikkurila L481	Tikkurila · Optiva 5 Matt	матовая	2	18	11,1 м²
	потолок		**К3**	Tikkurila F497	Tikkurila · Anti-Reflex 2	глубокомат.	2	88	14,6 м²
	пол		**КМ1**	по образцу	инженерная доска · аналог по хар.				14,6 м²
	плинтус		**К4**	Tikkurila F497	МДФ · в цвет Tikkurila	полуглянц.	2	88	15,6 м
12. Гардеробная 1 2,83 м²	стены		**К1**	Tikkurila F497	Tikkurila · Optiva 5 Matt	матовая	2	88	15,0 м²
	потолок		**К3**	Tikkurila F497	Tikkurila · Anti-Reflex 2	глубокомат.	2	88	2,8 м²
	пол		**КМ1**	по образцу	инженерная доска · аналог по хар.				2,8 м²
	плинтус		**К4**	Tikkurila F497	МДФ · в цвет Tikkurila	полуглянц.	2	88	5,5 м
13. Балкон 1 3,7 м²	стены		**К9**	Tikkurila F497	Tikkurila · Luja 7	полуматов.	1	88	16,5 м²
	потолок		**К5**	Tikkurila F497	Tikkurila · Luja 7	матовая	1	88	3,7 м²
	пол		**КМ6**	тон Claystone V486 (грейж)	керамогранит · аналог по хар.				3,7 м²
	плинтус		**КМ7**	тон Claystone V486 (грейж)	керамогранит · аналог по хар.				7,7 м

Условные обозначения

- **К1** Tikkurila F497 · Paper · Optiva 5 Matt · матовая · кл. 2
- **К2** Tikkurila L481 · Silhouette · Optiva 5 Matt · матовая · кл. 2
- **К3** Tikkurila F497 · Paper · Anti-Reflex 2 · глубокомат. · кл. 2
- **К4** Tikkurila F497 · Paper · МДФ · полуглянц. · кл. 2
- **К5** Tikkurila F497 · Paper · Luja 7 · матовая · кл. 1
- **К6** Tikkurila F497 · Paper · Joker · полуматов. · кл. 2
- **К7** Tikkurila J484 · Castle · Optiva 20 Semimatt · полуматов. · кл. 2
- **К8** Tikkurila J484 · Castle · МДФ · полуглянц. · кл. 2
- **К9** Tikkurila F497 · Paper · Luja 7 · полуматов. · кл. 1
- дерево (доска, паркет, ламинат) — рисунок досок
- керамогранит, плитка, камень — сетка швов по формату

- **КМ1** инженерная доска · аналог: дуб натуральный брашированный, масло-воск, 14/4 мм
- **КМ2** плитка · аналог: керамогранит матовый, тон F497, 600×600×9 мм
- **КМ3** аналог: керамогранит матовый R10, тон J484, 600×600×10 мм
- **КМ4** аналог: керамогранит матовый R10, тон V486, 600×600×10 мм
- **КМ5** аналог: керамогранит матовый, тон F497, 600×600×9 мм
- **КМ6** аналог: керамогранит матовый R11, тон V486, 600×600×10 мм
- **КМ7** керамогранит · аналог: плинтус из керамогранита пола, подрезка 80 мм, верхняя кромка с запилом 45°

К — краска, КМ — отделочный материал (тон КМ — по описанию, эталон — образец материала); кл. — класс истирания (1 — самый стойкий к мытью); LRV — светлота цвета: 0 — чёрный, 100 — белый

Перечень выкрасов на согласование

№	Код	Бренд / веер	Пом. / стена	Подложка	Формат	Статус
1	F497	Tikkurila Symphony / Feel the Colour	1	ГКЛ, загрунтованный под эту краску	600×1000	на согласов.
2	G503	Tikkurila Symphony / Feel the Colour	1	ГКЛ, загрунтованный под эту краску	600×1000	на согласов.
3	G497	Tikkurila Symphony / Feel the Colour	1	ГКЛ, загрунтованный под эту краску	600×1000	на согласов.
4	L481	Tikkurila Symphony / Feel the Colour	1 A	ГКЛ, загрунтованный под эту краску	600×1000	на согласов.
5	V477	Tikkurila Symphony / Feel the Colour	1 A	ГКЛ, загрунтованный под эту краску	600×1000	на согласов.
6	L462	Tikkurila Symphony / Feel the Colour	1 A	ГКЛ, загрунтованный под эту краску	600×1000	на согласов.
7	J484	Tikkurila Symphony / Feel the Colour	5	ГКЛ, загрунтованный под эту краску	600×1000	на согласов.
8	X487	Tikkurila Symphony / Feel the Colour	5	ГКЛ, загрунтованный под эту краску	600×1000	на согласов.
9	X463	Tikkurila Symphony / Feel the Colour	5	ГКЛ, загрунтованный под эту краску	600×1000	на согласов.

… ещё 2 выкрасов — в ведомости отделки

Примечания

1. Цвет на листе и на экране — ориентир. До покраски — выкрас на объекте: не меньше А3 (или лист ГКЛ), на грунте под эту краску, не на белой шпаклёвке, в 2 слоя; на обороте — код, бренд, веер, дата. Смотреть днём и вечером, рядом с образцами пола и плитки. Красить только в цвет утверждённого выкраса.
2. Краску заказывать по коду из графы «Система и код цвета» у бренда этого кода, не «аналогом» другого; весь объём одного кода — одной партией, колеруемую краску — за один проход машины.
3. Площади — те же, что в ведомости отделки (лист С1); сколько краски заказать — в спецификации отделочных материалов (лист С3).
4. Колерная карта на 2 листах: обозначения — на каждом, схема и палитра — на первом, выкрасы — на последнем.


	Лист	№ док.	Подпись	Дата	Проект: Четырёхкомнатная квартира			
Дизайнер	Кырлан А.С.			14.11.26	Колерная карта	Стадия	Лист	Листов
Проверил						П	31	147
Н. контр.								
Утв.								

Экспликация помещений

лист 22 · на плане — номера в марках

Ведомость мебели и оборудования

45 позиц. (48 шт.) — не помещается на листе:
полностью на листе 33 «Спецификация мебели и оборудования»
марка, наименование, Ш×Г×В, материал, модель,
допуск замены. Марки на плане — по ней.

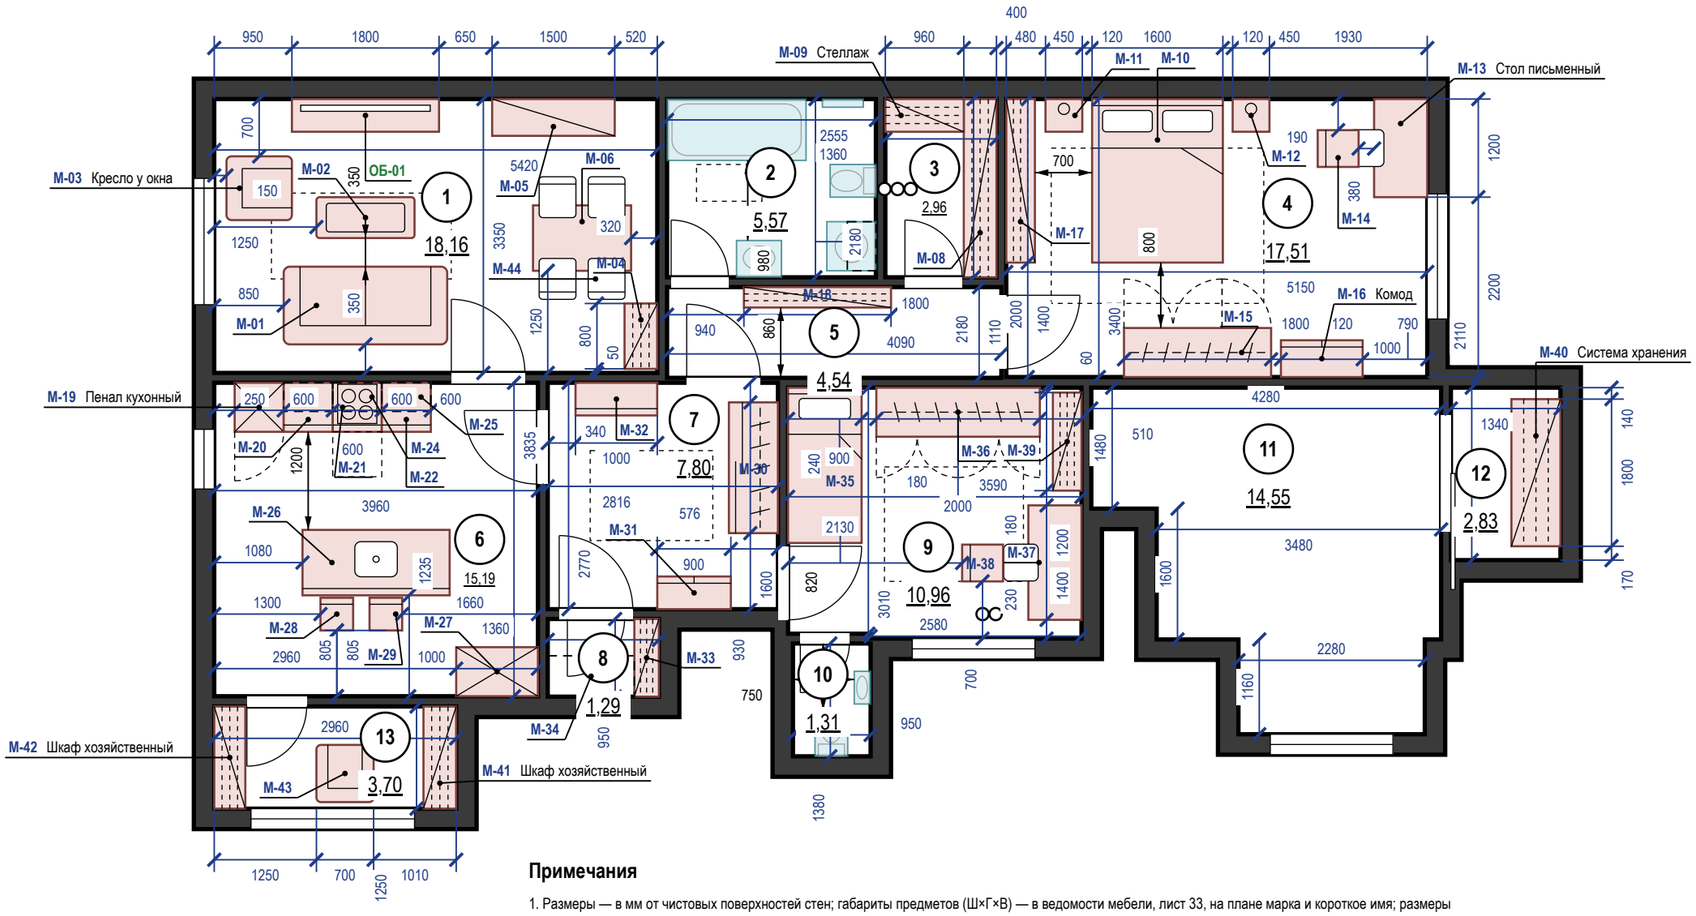

Примечания

1. Размеры — в мм от чистовых поверхностей стен; габариты предметов (Ш×Г×В) — в ведомости мебели, лист 33, на плане марка и короткое имя; размеры мебели уточнить после отделочных работ; общие указания — лист 19.
2. Отступ от стены, на плане не образмерен: М-43 — 80 мм.
3. У позиций М-07, М-23 марки на плане нет — места у предмета нет: позиция и габарит — в спецификации, лист 33.
4. У позиций ОБ-01, М-01, М-02, М-04, М-05, М-06, М-08, М-10, М-11, М-12, М-14, М-15, М-17, М-18, М-20, М-21, М-22, М-24, М-25, М-26, М-27, М-28, М-29, М-30, М-31, М-32, М-33, М-34, М-35, М-36, М-37, М-38, М-39, М-43, М-44 на плане только марка: наименование и габарит — в спецификации, лист 33.
5. Стулья обеденной группы (М-44 — 4 шт.) показаны в рабочем положении, задвинутыми под столешницу на 150 мм.

	Лист	№ док.	Подпись	Дата	Проект: Четырёхкомнатная квартира			М 1:75
Дизайнер	Кырлан А.С.			14.11.26	План размещения мебели и оборудования	Стадия	Лист	Листов
Проверил						П	32	147
Н. контр.								
Утв.								

Поз.	Наименование и техническая характеристика	Тип, марка, обозначение документа, опросного листа	Код продукции	Поставщик	Ед. измерения	Кол.	Масса 1 ед., кг	Примечание
	Мебель встроенная и корпусная (изготовление по чертежам мебельщика)							
М-07	Шкаф навесной над стиральной машиной; каркас и полки — ЛДСП 16 мм, декор «дуб натуральный»; без фасадов; Ш×Г×В 600×350×700 мм	—	—	изготовление на заказ	шт.	1	—	пом. 2; крепление к стене
М-08	Стеллаж хозяйственный, 6 полок; каркас и полки — ЛДСП 16 мм, декор «дуб натуральный»; без фасадов; Ш×Г×В 2180×400×2400 мм	—	—	изготовление на заказ	шт.	1	—	пом. 3; крепление к стене
М-09	Стеллаж хозяйственный, 6 полок; каркас и полки — ЛДСП 16 мм, декор «дуб натуральный»; без фасадов; Ш×Г×В 960×400×2400 мм	—	—	изготовление на заказ	шт.	1	—	пом. 3; крепление к стене
М-15	Шкаф распашной, 4 створки; корпус ЛДСП 16 мм; фасады — МДФ 18 мм, эмаль матовая; цвет фасадов — в цвет стен (Tikkurila F497); Ш×Г×В 1800×600×2400 мм	—	—	изготовление на заказ	шт.	1	—	пом. 4; крепление к стене
М-17	Стеллаж книжный открытый; каркас и полки — ЛДСП 16 мм, декор «дуб натуральный»; без фасадов; Ш×Г×В 2000×350×2100 мм	—	—	изготовление на заказ	шт.	1	—	пом. 4; крепление к стене
М-18	Шкаф хозяйственный неглубокий; корпус ЛДСП 16 мм; фасады — МДФ 18 мм, эмаль матовая; цвет фасадов — в цвет стен (Tikkurila J484); Ш×Г×В 1800×250×2400 мм	—	—	изготовление на заказ	шт.	1	—	пом. 5; крепление к стене
М-19	Пенал кухонный с встроенным холодильником; корпус ЛДСП 16 мм; фасады — МДФ 18 мм, эмаль матовая; цвет фасадов в цвет стен (Tikkurila F497); Ш×Г×В 600×600×2300 мм	—	—	изготовление на заказ	шт.	1	—	пом. 6; крепление к стене
М-20	Модуль нижний, ящики; корпус ЛДСП 16 мм; фасады — МДФ 18 мм, эмаль матовая; цвет фасадов — в цвет стен (Tikkurila F497); Ш×Г×В 600×600×900 мм	—	—	изготовление на заказ	шт.	1	—	пом. 6
М-21	Модуль нижний: варочная панель и духовой шкаф; корпус ЛДСП 16 мм; фасады — МДФ 18 мм, эмаль матовая; цвет фасадов — в цвет стен (Tikkurila F497); Ш×Г×В 600×600×900 мм	—	—	изготовление на заказ	шт.	1	—	пом. 6
М-22	Модуль нижний, ящики и бутылочница; корпус ЛДСП 16 мм; фасады — МДФ 18 мм, эмаль матовая; цвет фасадов — в цвет стен (Tikkurila F497); Ш×Г×В 600×600×900 мм	—	—	изготовление на заказ	шт.	1	—	пом. 6
М-23	Модуль навесной, 2 секции; корпус ЛДСП 16 мм; фасады — МДФ 18 мм, эмаль матовая; цвет фасадов — в цвет стен (Tikkurila F497); Ш×Г×В 600×350×720 мм	—	—	изготовление на заказ	шт.	1	—	пом. 6
М-24	Вытяжка встраиваемая в шкаф; корпус ЛДСП 16 мм; фасады — МДФ 18 мм, эмаль матовая; цвет фасадов — в цвет стен (Tikkurila F497); Ш×Г×В 600×350×600 мм	—	—	изготовление на заказ	шт.	1	—	пом. 6
М-25	Модуль навесной, 2 секции; корпус ЛДСП 16 мм; фасады — МДФ 18 мм, эмаль матовая; цвет фасадов — в цвет стен (Tikkurila F497); Ш×Г×В 600×350×720 мм	—	—	изготовление на заказ	шт.	1	—	пом. 6
М-26	Остров кухонный с мойкой и посудомоечной машиной; корпус ЛДСП 16 мм; фасады — МДФ 18 мм, эмаль матовая; цвет фасадов — в цвет стен (Tikkurila F497); Ш×Г×В 1800×800×900 мм	—	—	изготовление на заказ	шт.	1	—	пом. 6
М-27	Пенал-кладовая кухонная; корпус ЛДСП 16 мм; фасады — МДФ 18 мм, эмаль матовая; цвет фасадов — в цвет стен (Tikkurila F497); Ш×Г×В 1000×600×2300 мм	—	—	изготовление на заказ	шт.	1	—	пом. 6; крепление к стене
М-30	Шкаф-купе, 2 двери; корпус ЛДСП 16 мм; фасады — ЛДСП 10 мм в алюминиевом профиле; Ш×Г×В 1600×600×2400 мм	—	—	изготовление на заказ	шт.	1	—	пом. 7; крепление к стене
М-33	Система хранения: штанга, полки, ящики; каркас и полки — ЛДСП 16 мм, декор «дуб натуральный»; без фасадов; Ш×Г×В 950×300×2400 мм	—	—	изготовление на заказ	шт.	1	—	пом. 8; крепление к стене
М-34	Антресоль над зоной открывания двери; каркас и полки — ЛДСП 16 мм, декор «дуб натуральный»; без фасадов; Ш×Г×В 1060×500×300 мм	—	—	изготовление на заказ	шт.	1	—	пом. 8; крепление к стене
М-36	Шкаф распашной, 4 секции; корпус ЛДСП 16 мм; фасады — МДФ 18 мм, эмаль матовая; цвет фасадов — в цвет стен (Tikkurila F497); Ш×Г×В 2000×600×2400 мм	—	—	изготовление на заказ	шт.	1	—	пом. 9; крепление к стене
М-40	Система хранения торцевая: штанги, полки; каркас и полки — ЛДСП 16 мм, декор «дуб натуральный»; без фасадов; Ш×Г×В 1800×600×2400 мм	—	—	изготовление на заказ	шт.	1	—	пом. 12; крепление к стене
М-41	Шкаф хозяйственный балконный; каркас и полки — ЛДСП 16 мм, декор «дуб натуральный»; без фасадов; Ш×Г×В 1250×400×2000 мм	—	—	изготовление на заказ	шт.	1	—	пом. 13; крепление к стене
М-42	Шкаф хозяйственный балконный; каркас и полки — ЛДСП 16 мм, декор «дуб натуральный»; без фасадов; Ш×Г×В 1250×380×2000 мм	—	—	изготовление на заказ	шт.	1	—	пом. 13; крепление к стене

Примечания

1. Позиции мебели совпадают с марками на плане расстановки; размеры Ш×Г×В — Ш вдоль стены, Г от стены.
2. Размеры и привязки плана расстановки — в мм от чистовых поверхностей стен: слой штукатурки 20 мм по блоку и 5 мм шпаклёвки по ГКЛ учтён; привязки — от стен и углов помещения, а не от другой мебели.
3. План расстановки не является документацией для изготовления мебели. Встроенная и корпусная мебель изготавливается по чертежам мебельщика после контрольного обмера (после штукатурки); «стена в стену» — с зазором 10 мм с каждой стороны или с компенсаторами; графы «Тип, марка» и «Код продукции» для неё не заполняются (ГОСТ 21.110-2013).
4. Покупные изделия — аналог по характеристикам: заменять только на изделия не больше указанного габарита и того же материала и цвета.
5. Материал и цвет, не указанные в данных изделия, приняты по концепции: тон дерева — по полу, обивка — по вторичному цвету палитры; образцы согласовать до заказа.
6. Масса 1 ед. для изделий до 25 кг не указывается. Техника — по монтажным схемам изготовителя; выводы — по листам ЭОМ и ВК.

	Лист	№ док.	Подпись	Дата
Дизайнер	Кырлан А.С.			14.11.26
Проверил				
Н. контр.				
Утв.				

Проект: Четырёхкомнатная квартира

Спецификация мебели и оборудования

Стадия	Лист	Листов
П	33	147

Поз.	Наименование и техническая характеристика	Тип, марка, обозначение документа, опросного листа	Код продукции	Поставщик	Ед. измерения	Кол.	Масса 1 ед., кг	Примечание
	Мебель покупная							
М-01	Диван прямой трёхместный; обивка букле; Ш×Г×В 2000×950×800 мм	диван прямой, глубокая посадка, съёмные чехлы	—	аналог по характеристикам	шт.	1	—	пом. 1; допуск замены Ш 1900–2100, Г ≤ 1000
М-02	Стол журнальный; дерево — дуб натуральный; Ш×Г×В 1200×500×400 мм	стол журнальный прямоугольный	—	аналог по характеристикам	шт.	1	—	пом. 1; допуск замены Ш 1100–1300
М-03	Кресло у окна; обивка — ткань, цвет Tikkurila V486; Ш×Г×В 780×800×780 мм	кресло мягкое на деревянных ножках	—	аналог по характеристикам	шт.	1	—	пом. 1; допуск замены Ш 750–850, В ≤ 790 (не выше подоконника)
М-04	Стеллаж-витрина; дерево — дуб натуральный, металл — чёрный матовый; Ш×Г×В 800×400×2100 мм	стеллаж открытый, 5 полок	—	аналог по характеристикам	шт.	1	—	пом. 1; крепление к стене; допуск замены Ш 750–850
М-05	Буфет обеденной зоны; дерево — дуб натуральный, металл — чёрный матовый; Ш×Г×В 1500×450×900 мм	буфет 3-дверный	—	аналог по характеристикам	шт.	1	—	пом. 1; крепление к стене; допуск замены Ш 1400–1600, Г ≤ 470
М-06	Стол обеденный на 6 персон; дерево — дуб натуральный; Ш×Г×В 1200×800×750 мм	стол обеденный прямоугольный, раскладной до 1800	—	аналог по характеристикам	шт.	1	—	пом. 1; допуск замены Ш 1200–1400 в сложенном виде, Г 800–900
М-44	Стул обеденный к столу М-06; обивка — ткань, цвет Tikkurila V486; каркас — дуб натуральный; Ш×Г×В 450×500×820 мм	аналог: Ш×Г×В 450×500×820 мм, обивка — ткань	—	аналог по характеристикам	шт.	4	—	пом. 1; замена ≤ габарита
ОБ-01	ТВ-тумба с экраном 55" диагональ 55"; крепление — настенный кронштейн по паспорту модели; Ш×Г×В 1800×400×500 мм	тумба ТВ подвесная, 3 ящика	—	аналог по характеристикам	шт.	1	—	пом. 1; допуск замены Ш 1700–1900, Г ≤ 450
М-10	Кровать 1600×2000; мягкое изголовье, обивка — ткань, цвет Tikkurila V486; Ш×Г×В 1600×2000×450 мм	кровать с мягким изголовьем	—	аналог по характеристикам	шт.	1	—	пом. 4; допуск замены Ш 1600, Д 2000–2050
М-11, М-12	Тумба прикроватная; дерево — дуб натуральный; Ш×Г×В 450×400×550 мм	тумба прикроватная, 2 ящика	—	аналог по характеристикам	шт.	2	—	пом. 4; допуск замены Ш 400–500
М-13	Стол письменный у окна; дерево — дуб натуральный, металл — чёрный матовый; Ш×Г×В 1200×650×750 мм	стол письменный с тумбой	—	аналог по характеристикам	шт.	1	—	пом. 4; допуск замены Ш 1100–1300, Г 600–700
М-14, М-38	Кресло рабочее; металл — чёрный матовый; Ш×Г×В 450×500×950 мм	кресло рабочее на роликах	—	аналог по характеристикам	шт.	2	—	пом. 4, 9; допуск замены Ш 480–560
М-16	Комод, 4 ящика; дерево — дуб натуральный; Ш×Г×В 1000×450×850 мм	комод 4 ящика	—	аналог по характеристикам	шт.	1	—	пом. 4; крепление к стене; допуск замены Ш 950–1100
М-28, М-29	Стул полубарный Н 650 у острова, каркас — чёрный металл, сиденье — дуб натуральный; дерево — дуб натуральный, металл — чёрный матовый; Ш×Г×В 400×400×900 мм	аналог: Ш×Г×В 400×400×900 мм, дерево — дуб натуральный	—	аналог по характеристикам	шт.	2	—	пом. 6; замена ≤ габарита
М-31	Банкетка-обувница с мягким сиденьем; дерево — дуб натуральный; Ш×Г×В 900×400×450 мм	банкетка-обувница	—	аналог по характеристикам	шт.	1	—	пом. 7; допуск замены Ш 800–950
М-32	Консоль прихожей, 3 ящика; дерево — дуб натуральный, металл — чёрный матовый; Ш×Г×В 1000×400×850 мм	консоль-комод	—	аналог по характеристикам	шт.	1	—	пом. 7; крепление к стене; допуск замены Ш 950–1100
М-35	Кровать 900×1900; мягкое изголовье, обивка — ткань, цвет Tikkurila V486; Ш×Г×В 900×1900×450 мм	кровать односпальная с мягким изголовьем	—	аналог по характеристикам	шт.	1	—	пом. 9; допуск замены Ш 900, Д 1900–1950
М-37	Стол письменный у стены Б, рядом с окном стены В: свет боковой; дерево — дуб натуральный, металл — чёрный матовый; Ш×Г×В 1400×650×750 мм	стол письменный с тумбой	—	аналог по характеристикам	шт.	1	—	пом. 9; допуск замены Ш 1300–1500, Г 600–700
М-39	Стеллаж книжный; дерево — дуб натуральный; Ш×Г×В 1200×350×2100 мм	аналог: Ш×Г×В 1200×350×2100 мм, дерево — дуб натуральный	—	аналог по характеристикам	шт.	1	—	пом. 9; крепление к стене; замена ≤ габарита
М-43	Кресло балконное; металл — чёрный матовый; Ш×Г×В 700×700×780 мм	кресло на металлическом каркасе	—	аналог по характеристикам	шт.	1	—	пом. 13; допуск замены Ш 650–750, В ≤ 850 (не выше подоконника)

	Лист	№ док.	Подпись	Дата
Дизайнер	Кырлан А.С.			14.11.26
Проверил				
Н. контр.				
Утв.				

Проект: Четырёхкомнатная квартира

Спецификация мебели и оборудования (продолжение)

Стадия	Лист	Листов
П	34	147

Поз.	Наименование и техническая характеристика	Тип, марка, обозначение документа, опросного листа	Код продукции	Поставщик	Ед. измерения	Кол.	Масса 1 ед., кг	Примечание
	Техника встраиваемая и бытовая (покупные изделия), светильники под розетки							
	Стиральная машина встраиваемая, у М-07	аналог по характеристикам: тип загрузки — по листу ВК, по листу ВК	—	по выбору заказчика до изготовления мебели	шт.	1	—	пом. 2; по схеме изготовителя
	Холодильник встраиваемый, в модуле М-19	аналог по характеристикам: полновстраиваемый под фасад, ниша 1780 × 560 × 550 мм, вентиляция решётка в цоколе, выход сверху	—	по выбору заказчика до изготовления мебели	шт.	1	—	пом. 6; по схеме изготовителя
	Духовой шкаф встраиваемый, в модуле М-21	аналог по характеристикам: 60 см, лицевая панель 595 мм, ниша 560 × 600, глубина ≥ 550 мм, вентиляция за прибором	—	по выбору заказчика до изготовления мебели	шт.	1	—	пом. 6; по схеме изготовителя
	Вытяжка встраиваемая, в модуле М-24	аналог по характеристикам: производительность — по расчёту ОВ, шум ≤ 55 дБ(А)	—	по выбору заказчика до изготовления мебели	шт.	1	—	пом. 6; по схеме изготовителя
	Посудомоечная машина встраиваемая, в модуле М-26; ниша 600 мм	аналог по характеристикам: полновстраиваемая 60 см под фасад, ниша 600 × по высоте ряда мм, навеска фасада в комплекте	—	по выбору заказчика до изготовления мебели	шт.	1	—	пом. 6; по схеме изготовителя
	Варочная панель встраиваемая, индукционная, в модуле М-21	аналог по характеристикам: индукционная 60 см, вырез 560 × 490 мм по шаблону модели	—	по выбору заказчика до изготовления мебели	шт.	1	—	пом. 6; по схеме изготовителя
	Торшер, у поз. М-01; абажур — ткань или опаловое стекло; лампа 2700 К	—	—	аналог по характеристикам	шт.	1	—	пом. 1; розетка Р3 (ЭОМ)
	Текстиль							
Т1	Портьеры-волна, два полотна; лён 100 %; цвет Tikkurila V486; карниз 2150 мм, высота 2690 мм, сборка 2	—	—	аналог по характеристикам	шт.	2	—	пом. 1
Т2	Тюль-вуаль, одно полотно; полиэстер 100 %; цвет Tikkurila F497; карниз 2150 мм, высота 2690 мм, сборка 2,5	—	—	аналог по характеристикам	шт.	1	—	пом. 1
Т3	Ковёр мягкой группы; шерсть 100 %; цвет NCS S 3005-Y20R; 2200×1050 мм	—	—	аналог по характеристикам	шт.	1	—	пом. 1; с подложкой
Т4	Подушки декоративные на диван; лён 100 %; цвет Tikkurila H487	—	—	аналог по характеристикам	шт.	2	—	пом. 1
Т5	Подушки декоративные на диван, акцент; хлопковый бархат 100 %; цвет Tikkurila L481	—	—	аналог по характеристикам	шт.	2	—	пом. 1
Т6	Плед на диван; шерсть мериноса 100 %; цвет Tikkurila L481	—	—	аналог по характеристикам	шт.	1	—	пом. 1
Т7	Раннер на обеденный стол; лён 100 %; цвет Tikkurila J484	—	—	аналог по характеристикам	шт.	1	—	пом. 1
Т24	Полотенца банные махровые, коричнево-лиловые, сложены на полотенцесушителе; хлопок 100 %; цвет Tikkurila L481	—	—	аналог по характеристикам	шт.	2	—	пом. 2
Т25	Полотенца для рук вафельные, тёплый белый, на нижних перекладинах сушителя; хлопок 100 %; цвет Tikkurila F497	—	—	аналог по характеристикам	шт.	2	—	пом. 2
Т26	Ковёр — коврик для ванной у бортика ванны, хлопок тафтинг, грейж; хлопок 100 %, латексная противоскользящая основа; цвет Tikkurila V486; 800×450 мм	—	—	аналог по характеристикам	шт.	1	—	пом. 2; с подложкой
Т8	Портьеры стационарные, два полотна; лён 55 %, хлопок 45 %; цвет Tikkurila V484; карниз 2140 мм, высота 2690 мм, сборка 2	—	—	аналог по характеристикам	шт.	2	—	пом. 4
Т9	Римская штора блэкаут: окно закрывает она, стол М-13 у окна не мешает; хлопок 100 %, подкладка полиэстер; цвет Tikkurila H487; карниз 1650 мм, высота 1900 мм	—	—	аналог по характеристикам	шт.	1	—	пом. 4
Т10	Ковёр у кровати; шерсть 80 %, хлопок 20 %; цвет Tikkurila H487; 2600×1900 мм	—	—	аналог по характеристикам	шт.	1	—	пом. 4; с подложкой
Т11	Подушки декоративные на кровать; лён 100 %; цвет Tikkurila H487	—	—	аналог по характеристикам	шт.	2	—	пом. 4
Т12	Подушка декоративная, акцент; хлопковый бархат 100 %; цвет NCS S 5010-B10G	—	—	аналог по характеристикам	шт.	1	—	пом. 4
Т13	Плед на кровать; хлопок 100 %; цвет NCS S 5010-B10G	—	—	аналог по характеристикам	шт.	1	—	пом. 4
Т14	Рулонная штора кассетная, ткань димаут; полиэстер 100 %; цвет Tikkurila J484; карниз 890 мм, высота 1900 мм	—	—	аналог по характеристикам	шт.	1	—	пом. 6

	Лист	№ док.	Подпись	Дата	Проект: Четырёхкомнатная квартира			
Дизайнер	Кырлан А.С.			14.11.26				
Проверил					Спецификация мебели и оборудования (продолжение)	Стадия	Лист	Листов
Н. контр.						П	35	147
Утв.								

Поз.	Наименование и техническая характеристика	Тип, марка, обозначение документа, опросного листа	Код продукции	Поставщик	Ед. измерения	Кол.	Масса 1 ед., кг	Примечание
Т15	Ковёр прихожей, низкий ворс; шерсть 80 %, полиамид 20 %; цвет NCS S 3005-Y20R; 1500×1100 мм	—	—	аналог по характеристикам	шт.	1	—	пом. 7; с подложкой
Т16	Портьеры стационарные, два полотна, до подоконника: радиатор под окном открыт; лён 55 %, хлопок 45 %; цвет Tikkurila V484; карниз 1800 мм, высота 1930 мм, сборка 2	—	—	аналог по характеристикам	шт.	2	—	пом. 9
Т17	Римская штора блэкаут: закрывает проём целиком, радиатор под окном не задевает; хлопок 100 %, подкладка полиэстер; цвет Tikkurila H487; карниз 1620 мм, высота 1900 мм	—	—	аналог по характеристикам	шт.	1	—	пом. 9
Т18	Ковёр игровой зоны; шерсть 100 %; цвет NCS S 3005-Y20R; 1700×1400 мм	—	—	аналог по характеристикам	шт.	1	—	пом. 9; с подложкой
Т19	Подушки декоративные на кровать; лён 100 %; цвет Tikkurila H487	—	—	аналог по характеристикам	шт.	2	—	пом. 9
Т20	Подушка декоративная, акцент; шерсть 60 %, полиэстер 40 %; цвет Farrow & Ball No. 47	—	—	аналог по характеристикам	шт.	1	—	пом. 9
Т21	Плед на кровать; хлопок 100 %; цвет Farrow & Ball No. 47	—	—	аналог по характеристикам	шт.	1	—	пом. 9
Т22	Рулонная штора кассетная, солнцезащитная; полиэстер 100 %; цвет Tikkurila V486; карниз 2140 мм, высота 1700 мм	—	—	аналог по характеристикам	шт.	1	—	пом. 13
Т23	Плед на кресло М-43; шерсть 100 %; цвет Tikkurila V484	—	—	аналог по характеристикам	шт.	1	—	пом. 13
	Декор							
ДК1	Картина над диваном: крупная абстракция, холст, тонкая рама; 1400×900 мм; низ на 1000 мм от пола	—	—	аналог по характеристикам	шт.	1	6	пом. 1; крепление: планка на дюбелях, 4 точки
ДК2	Зеркало над буфетом, рама шпон дуба; 1000×800 мм; низ на 1100 мм от пола	—	—	аналог по характеристикам	шт.	1	12	пом. 1; крепление: анкер химический, 4 точки
ДК3	Фикус лировидный в кашпо Ø400; 450×450 мм	—	—	аналог по характеристикам	шт.	1	—	пом. 1
ДК29	Книги по искусству стопкой и свеча в керамической чаше на журнальном столе; 300×150 мм; на М-02	—	—	аналог по характеристикам	шт.	1	—	пом. 1
ДК30	Вазы ручной работы разной высоты (320 и 200 мм), 2 шт., глазурь серо-петроль, на буфете М-05 слева от зеркала; 220×320 мм; на М-05	—	—	аналог по характеристикам	шт.	2	—	пом. 1
ДК31	Ваза керамическая с ветками на обеденном столе, матовая глазурь, коричнево-лиловая; 200×300 мм; на М-06	—	—	аналог по характеристикам	шт.	1	—	пом. 1
ДК4	Зеркало над раковиной С-03, влагостойкое; 600×800 мм; низ на 1100 мм от пола	—	—	аналог по характеристикам	шт.	1	5	пом. 2; крепление: зеркалодержатели, 4 точки
ДК22	Ваза-бутыль глазурованная, коричнево-лиловая, с сухой веткой эвкалипта — на полке короба инсталляции; 130×400 мм	—	—	аналог по характеристикам	шт.	1	—	пом. 2
ДК23	Свеча в янтарном стекле и аромадиффузор с ротанговыми палочками на подносе — на полке короба; 150×180 мм	—	—	аналог по характеристикам	шт.	1	—	пом. 2
ДК5	Картина над изголовьем: графика, паспарту, рама; 1100×700 мм; низ на 1300 мм от пола	—	—	аналог по характеристикам	шт.	1	4	пом. 4; крепление: две петли на дюбелях
ДК6	Зеркало над комодом М-16; 700×900 мм; низ на 1050 мм от пола	—	—	аналог по характеристикам	шт.	1	8	пом. 4; крепление: анкер химический, 4 точки
ДК7	Хлорофитум хохлатый в напольном кашпо Ø380; 420×420 мм	—	—	аналог по характеристикам	шт.	1	—	пом. 4
ДК32	Лампа настольная рабочая на столе М-13: шарнирная стойка — чёрный металл, абажур-колпак; рама — чёрный матовый; 220×480 мм; на М-13	—	—	аналог по характеристикам	шт.	1	—	пом. 4
ДК33	Книги стопкой на тумбе М-11; 280×120 мм; на М-11	—	—	аналог по характеристикам	шт.	1	—	пом. 4
ДК34	Низкая чаша и шкатулка ручной работы, глазурь дымчатый зелёный, на комоде М-16; 240×170 мм; на М-16	—	—	аналог по характеристикам	шт.	1	—	пом. 4
ДК27	Диптих в коридоре, левый: линии прибоя, линогравюра в паспарту, рама — дуб, 500×700; 500×700 мм; низ на 1150 мм от пола	—	—	аналог по характеристикам	шт.	1	3	пом. 5; крепление: планка на дюбелях, 2 точки

	Лист	№ док.	Подпись	Дата
Дизайнер	Кырлан А.С.			14.11.26
Проверил				
Н. контр.				
Утв.				

Проект: Четырёхкомнатная квартира

Спецификация мебели и оборудования (продолжение)

Стадия	Лист	Листов
П	36	147

Поз.	Наименование и техническая характеристика	Тип, марка, обозначение документа, опросного листа	Код продукции	Поставщик	Ед. измерения	Кол.	Масса 1 ед., кг	Примечание
ДК28	Диптих в коридоре, правый: гряда холмов, линогравюра в паспарту, рама — дуб, 500×700; 500×700 мм; низ на 1150 мм от пола	—	—	аналог по характеристикам	шт.	1	3	пом. 5; крепление: планка на дюбелях, 2 точки
ДК8	Часы настенные Ø400; 400×400 мм; центр на 1550 мм от пола	—	—	аналог по характеристикам	шт.	1	2	пом. 6; крепление: дюбель с крюком, 1 точка
ДК9	Хлорофитум хохлатый на подоконнике (отм. +0,800); 300×200 мм; низ на 800 мм от пола	—	—	аналог по характеристикам	шт.	1	—	пом. 6
ДК36	Чаша для фруктов и кувшин ручной работы, глазурь коричнево-лиловая, на острове М-26; 300×280 мм; на М-26	—	—	аналог по характеристикам	шт.	1	—	пом. 6
ДК37	Ваза ручной работы с ветками, глазурь коричнево-лиловая, на столешнице кухни; 200×320 мм; на М-20	—	—	аналог по характеристикам	шт.	1	—	пом. 6
ДК10	Зеркало над консолью М-32; 700×1000 мм; низ на 1050 мм от пола	—	—	аналог по характеристикам	шт.	1	9	пом. 7; крепление: анкер химический, 4 точки
ДК11	Замиокулькас в напольном кашпо Ø360; 400×400 мм	—	—	аналог по характеристикам	шт.	1	—	пом. 7
ДК25	Чаша для ключей и низкая ваза ручной работы, глазурь серо-петроль, на консоли М-32; 260×170 мм; на М-32	—	—	аналог по характеристикам	шт.	1	—	пом. 7
ДК26	Графика на стене В справа от банкетки: ветка гинкго, линогравюра в паспарту, рама — дуб, 400×560; 400×560 мм; низ на 1220 мм от пола	—	—	аналог по характеристикам	шт.	1	2	пом. 7; крепление: планка на дюбелях, 2 точки
ДК12	Картина над изголовьем: графика, паспарту, рама; 600×800 мм; низ на 1200 мм от пола	—	—	аналог по характеристикам	шт.	1	3	пом. 9; крепление: две петли на дюбелях
ДК13	Постер в раме, левый (группа «постеры»); 400×500 мм; низ на 1250 мм от пола	—	—	аналог по характеристикам	шт.	1	2	пом. 9; крепление: петля на дюбеле
ДК14	Постер в раме, средний (группа «постеры»); 400×500 мм; низ на 1250 мм от пола	—	—	аналог по характеристикам	шт.	1	2	пом. 9; крепление: петля на дюбеле
ДК15	Постер в раме, правый (группа «постеры»); 400×500 мм; низ на 1250 мм от пола	—	—	аналог по характеристикам	шт.	1	2	пом. 9; крепление: петля на дюбеле
ДК16	Спатифиллум в напольном кашпо Ø360; 400×400 мм	—	—	аналог по характеристикам	шт.	1	—	пом. 9
ДК35	Лампа настольная рабочая на столе М-37: шарнирная стойка — чёрный металл, абажур-колпак; рама — чёрный матовый; 220×480 мм; на М-37	—	—	аналог по характеристикам	шт.	1	—	пом. 9
ДК17	Зеркало над раковиной С-07, влагостойкое; 500×700 мм; низ на 1150 мм от пола	—	—	аналог по характеристикам	шт.	1	4	пом. 10; крепление: зеркалодержатели, 4 точки
ДК24	Ваза-кувшин керамическая, дымчатый зелёный, с сухоцветом (лагурус) — на полке короба инсталляции; 130×380 мм	—	—	аналог по характеристикам	шт.	1	—	пом. 10
ДК20	Картина: тёмная лиловая абстракция, холст, тонкая рама; 800×600 мм; низ на 1300 мм от пола	—	—	аналог по характеристикам	шт.	1	4	пом. 11; крепление: планка на дюбелях, 2 точки
ДК21	Ваза напольная, керамика матовая; 300×300 мм	—	—	аналог по характеристикам	шт.	1	—	пом. 11
ДК18	Зеркало ростовое 500×1600; 500×1600 мм; низ на 250 мм от пола	—	—	аналог по характеристикам	шт.	1	12	пом. 12; крепление: анкер химический, 4 точки + опора снизу
ДК19	Лавр благородный в напольном кашпо Ø380; 400×400 мм	—	—	аналог по характеристикам	шт.	1	—	пом. 13

	Лист	№ док.	Подпись	Дата
Дизайнер	Кырлан А.С.			14.11.26
Проверил				
Н. контр.				
Утв.				

Проект: Четырёхкомнатная квартира

Спецификация мебели и оборудования (продолжение)

Стадия	Лист	Листов
П	37	147

Ведомость изделий

Марка	Наименование	Пом.	Ш×Г×В, мм	Корпус	Фасад	Кромка, мм	Кол.
М-07	Система хранения	2	600×350×700	ЛДСП 16	без фасадов	0,4 / 2	1
М-08	Система хранения	3	2180×400×2400	ЛДСП 16	без фасадов	0,4 / 2	1
М-09	Система хранения	3	960×400×2400	ЛДСП 16	без фасадов	0,4 / 2	1
М-15	Шкаф распашной	4	1800×600×2400	ЛДСП 16	МДФ 18 мм, эмаль матовая	0,4 / 2	1
М-17	Система хранения	4	2000×350×2100	ЛДСП 16	без фасадов	0,4 / 2	1
М-18	Система хранения	5	1800×250×2400	ЛДСП 16	МДФ 18 мм, эмаль матовая	0,4 / 2	1
М-30	Шкаф-купе	7	1600×600×2400	ЛДСП 16	ЛДСП 10 мм в алюминиевом профиле	0,4 / 2	1
М-33	Система хранения	8	950×300×2400	ЛДСП 16	без фасадов	0,4 / 2	1
М-34	Система хранения	8	1060×500×300	ЛДСП 16	без фасадов	0,4 / 2	1
М-36	Шкаф распашной	9	2000×600×2400	ЛДСП 16	МДФ 18 мм, эмаль матовая	0,4 / 2	1
М-40	Система хранения	12	1800×600×2400	ЛДСП 16	без фасадов	0,4 / 2	1
М-41	Система хранения	13	1250×400×2000	ЛДСП 16	без фасадов	0,4 / 2	1
М-42	Система хранения	13	1250×380×2000	ЛДСП 16	без фасадов	0,4 / 2	1
М-19	Пенал: холодильник встр.	6	600×600×2300	ЛДСП 16	МДФ 18 мм, эмаль матовая	0,4 / 2	1
М-20	Модуль нижний: ящики	6	600×600×900	ЛДСП 16	МДФ 18 мм, эмаль матовая	0,4 / 2	1
М-23	Модуль навесной: полки	6	600×350×720	ЛДСП 16	МДФ 18 мм, эмаль матовая	0,4 / 2	1
М-21	Модуль нижний: духовой шкаф, варочная	6	600×600×900	ЛДСП 16	МДФ 18 мм, эмаль матовая	0,4 / 2	1
М-24	Модуль навесной: полки	6	600×350×600	ЛДСП 16	МДФ 18 мм, эмаль матовая	0,4 / 2	1
М-22	Модуль нижний: ящики	6	600×600×900	ЛДСП 16	МДФ 18 мм, эмаль матовая	0,4 / 2	1
М-25	Модуль навесной: полки	6	600×350×720	ЛДСП 16	МДФ 18 мм, эмаль матовая	0,4 / 2	1
М-27	Пенал: полки	6	1000×600×2300	ЛДСП 16	МДФ 18 мм, эмаль матовая	0,4 / 2	1
М-26	Остров (М-26.1, М-26.2, М-26.3)	6	1800×800×900	ЛДСП 16	МДФ 18 мм, эмаль матовая	0,4 / 2	1

Ведомость встраиваемой техники

Поз.	Прибор	Ниша, вырез, мм	Вентиляция	Питание	Схема
М-19	Холодильник встраиваемый, ниша 1780	ниша 1780 × 560 × 550	решётка в цоколе, канал за корпусом, выход сверху	Р20: М-20, Н=150 — в соседнем модуле, за ящиком	по модели
М-21	Духовой шкаф встраиваемый, 60 см	ниша 560 × 600, глубина ≥ 550	зазор за шкафом, вырез в задней стенке	ЭВ4: М-22, Н=150 — в соседнем модуле, за ящиком	по модели
М-21	Варочная панель индукционная, 60 см	вырез в столешнице 560 × 490		ЭВ3: М-20, Н=150 — в соседнем модуле, за ящиком	по модели
М-24	Вытяжка встраиваемая в навесной модуль, 60 см	низ ≥ 650 над панелью	воздуховод к вентканалу, короб до потолка	Р21: М-24, Н=2200 — в навесном модуле	по модели
М-26.2	Мойка врезная / подстольная с сифоном	вырез по шаблону, ориентир 760 × 480		смеситель — выводы ВК	по модели

Ведомость фурнитуры

№	Фурнитура	Тип, размер	Изделия	Кол.
1	Полкодержатель с фиксацией	ø5 мм	М-07, М-08, М-09, М-15, М-17, М-18, М-30, М-33, М-36, М-40, М-41, М-42, М-19, М-23, М-24, М-25, М-27	328
2	Анкер по основанию стены	по таблице крепежа	М-07, М-08, М-09, М-15, М-17, М-18, М-30, М-33, М-34, М-36, М-40, М-41, М-42, М-23, М-24, М-25	95
3	Уголок крепления к стене от опрокидывания	стальной	М-07, М-08, М-09, М-15, М-17, М-18, М-30, М-33, М-34, М-36, М-40, М-41, М-42, М-19, М-27	30
4	Штанга выдвижная торцевая	L по глубине	М-08, М-09, М-17, М-41, М-42	9
5	Опора регулируемая с цоколем на клипсах	ход 20 мм	М-08, М-09, М-15, М-17, М-18, М-30, М-33, М-36, М-40, М-41, М-42	78
6	Петля накладная 110° с доводчиком	чашка 35 мм	М-15, М-18, М-36, М-19, М-23, М-24, М-25, М-27, М-26	100
7	Штанга овальная 30×15, L = 876	+ 2 держателя	М-15	1
8	Система дверей купе: профиль, направляющие, ролики	на 2 двери	М-30	1
9	Ручка-профиль вертикальная	в цвет профиля	М-30	2
10	Штанга овальная 30×15, L = 776	+ 2 держателя	М-30	1
11	Полка для обуви выдвижная наклонная	ширина 776	М-30	3
12	Штанга овальная 30×15, L = 976	+ 2 держателя	М-36	1
13	Штанга овальная 30×15, L = 579	+ 2 держателя	М-40	3
14	Ручка-профиль	латунь матовая	М-19, М-20, М-23, М-21, М-24, М-22, М-25, М-27, М-26	26
15	Опора кухонная регулируемая 100–120 мм	+ клипса цоколя	М-19, М-20, М-21, М-22, М-27, М-26	34
16	Направляющие полного выдвижения с доводчиком NL 500	пара	М-20, М-21, М-22, М-26	13
17	Навес регулируемый для навесного шкафа	пара на секцию	М-23, М-24, М-25	3
18	Шина монтажная	L = 540	М-23, М-24, М-25	3
19	Уголок крепления острова к полу	стальной, в цоколе	М-26	4


Примечания

1. Модели техники выбирает заказчик до изготовления мебели; ниши, вырезы и вентиляция — по монтажной схеме выбранной модели (условие гарантии), её номер вносится в ведомость.
2. Количество фурнитуры — по чертежам изделий; запас крепежа 5 %. Аналоги — по характеристикам (доводчик, нагрузка, ход).
3. Цвет корпусов, фасадов и профилей — по колерной карте проекта. Кромка — скрытые / видимые торцы, мм.


	Лист	№ док.	Подпись	Дата	Проект: Четырёхкомнатная квартира			
Дизайнер	Кырлан А.С.			14.11.26	Ведомости изделий, техники и фурнитуры	Стадия	Лист	Листов
Проверил						П	38	147
Н. контр.								
Утв.								

выпуск 14.11.2026 № e7147312ff · стр. 38 из 147


Фрагмент 1. Ванная комната, пом. 2 (М 1:50)

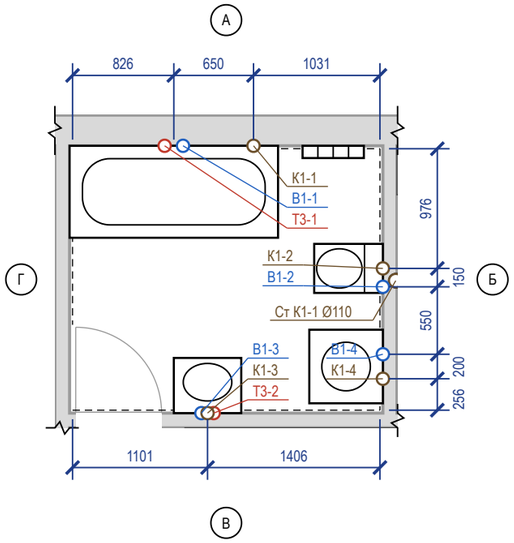

Фрагмент 2. Кухня, пом. 6 (М 1:50)

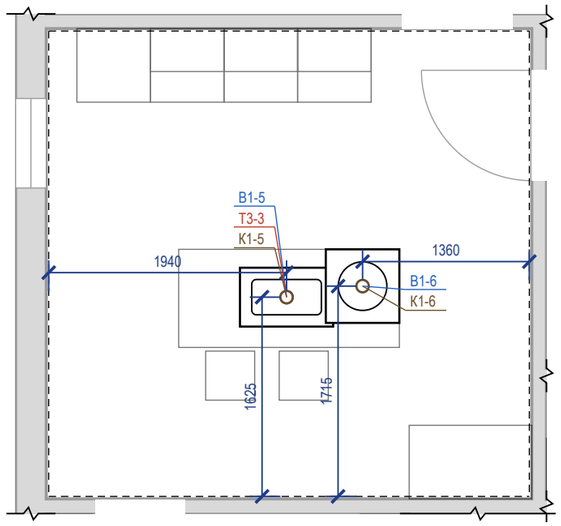

Фрагмент 3. Санузел, пом. 10 (М 1:50)

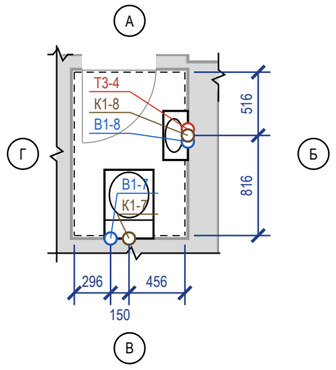

Ведомость привязок выводов

Код	Прибор	Ø	H, мм	Привязка от чист. стен, мм	Прим.
В1-1	С-01 ванна	½"	800	ст. А: 901 от Г	межос. 150
Т3-1	—"	½"	800	ст. А: 751 от Г	межос. 150
К1-1	—"	Ø50	60	ст. А: 1031 от Б	
В1-2	С-02 унитаз подвесной	½"	250	ст. Б: 1006 от В	в раме инсталляции
К1-2	—"	Ø110	220	ст. Б: 976 от А	
В1-3	С-03 умывальник	½"	550	ст. В: 1051 от Г	межос. 100
Т3-2	—"	½"	550	ст. В: 1151 от Г	межос. 100
К1-3	—"	Ø40	450	ст. В: 1101 от Г	
В1-4	ОБ-02 стиральная машина	½"	700	ст. Б: 456 от В	кран машины
К1-4	—"	Ø40	700	ст. Б: 256 от В	
В1-5	С-05 мойка кухонная	½"	600	1940 от Г; 1625 от В	межос. 100
Т3-3	—"	½"	600	1940 от Г; 1625 от В	межос. 100
К1-5	—"	Ø50	400	1940 от Г; 1625 от В	
В1-6	ОБ-03 посудомоечная машина	½"	550	1360 от Б; 1715 от В	кран ПММ
К1-6	—"	Ø50	550	1360 от Б; 1715 от В	
В1-7	С-06 унитаз подвесной	½"	250	ст. В: 296 от Г	в раме инсталляции
К1-7	—"	Ø110	220	ст. В: 446 от Г	
В1-8	С-07 умывальник	½"	550	ст. Б: 566 от А	межос. 100
Т3-4	—"	½"	550	ст. Б: 466 от А	межос. 100
К1-8	—"	Ø40	450	ст. Б: 516 от А	

Условные обозначения

- вывод В1 (код — в ведомости привязок)
- вывод Т3 (код — в ведомости привязок)
- вывод К1 (код — в ведомости привязок)
- сантехприбор по расстановке (габарит модели)
- чистовая поверхность стены (от неё привязки)
- стояк «Ст К1-N / Ст В1-N» (ГОСТ 21.601), Ø мм
- стояк Т3 не на обмере — принят в шахте рядом со Ст В1, сверить
- линия обрыва (граница фрагмента)
- А — обозначение стены А–Г (как на развёртках)


Примечания

1. Привязки выводов даны от чистовых поверхностей стен (облицовка на сторону: ванная комната — 24 мм (штукатурка 10 + клей 5 + плитка 9); кухня — 20 мм (по данным); санузел — 24 мм (штукатурка 10 + клей 5 + плитка 9)); эти же грани — на развёртках и в раскладке плитки. Высоты — от чистого пола помещения.
2. До черновой разводки сверить по паспорту выбранного прибора (смеситель, инсталляция, сифон).
3. Горячая вода (Т3) — слева от холодной (В1), если смотреть на прибор. Допуск установки выводов: ±5 мм в группе, ±20 мм у отдельно стоящих.
4. Расчёт систем водоснабжения и канализации и подбор оборудования выполняет проектная организация; лист задаёт места и высоты выводов.
5. С-05 мойка кухонная (В1-5, Т3-3, К1-5) — выводы в полу: пирог пола 170 мм их не укрывает (нужно 307 мм, расчёт — профиль К1 схемы разводки); до решения заказчика (подъём пола или другой смеситель / выпуск) не выполнять.
6. ОБ-03 посудомоечная машина (В1-6, К1-6) — выводы в полу: пирог пола 170 мм их не укрывает (нужно 257 мм, расчёт — профиль К1 схемы разводки); до решения заказчика (подъём пола или другой смеситель / выпуск) не выполнять.
7. Ст Т3-2 на обмере не показаны: приняты рядом с Ст В1-2 (в МКД стоят группой); положение сверить на объекте до разметки.
8. Стояки в коробах/шахтах не замоноличивать; стояк К1 в коробе — звукоизоляция стояка в коробе без жёсткого контакта с трубой; к арматуре и ревизиям — люк не меньше 300×400.
9. Штриховая линия чистовой грани стены прерывается на длине полотна открытой двери, лежащего вдоль грани (линии не должны сливаться при печати); положение грани — по размерам, а не по штриху.


	Лист	№ док.	Подпись	Дата	Проект: Четырёхкомнатная квартира			М 1:50
Дизайнер	Кырлан А.С.			14.11.26	План выводов сантехники	Стадия	Лист	Листов
Проверил						П	39	147
Н. контр.								
Утв.								

выпуск 14.11.2026 № e7147312ff · стр. 39 из 147


План квартиры (М 1:400)

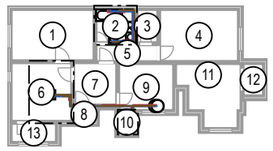


Фр. 1. Ванная комната (М 1:40)

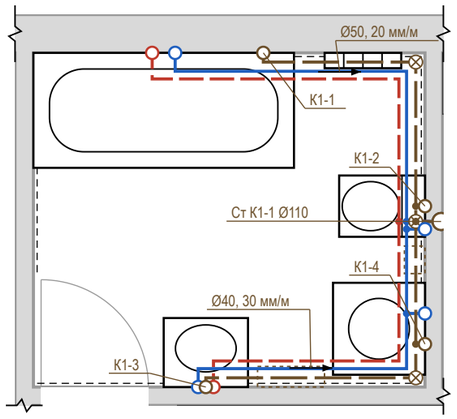

Фр. 2. Кухня (М 1:40)

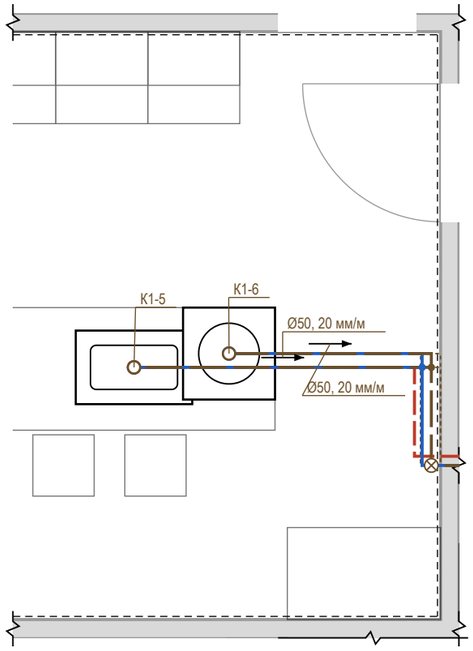

Фр. 3. Санузел (М 1:40)

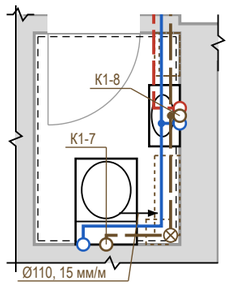

Условные обозначения


- В1 — водопровод хозяйственно-питьевой (ХВС), PP-R Ø20
- Т3 — горячее водоснабжение, подача (ГВС), PP-R Ø20
- К1 — канализация бытовая
- направление уклона К1 / пола: Ø, мм на 1 м
- ⊗ ревизия (прочистка) К1 — доступ сохранить
- • тройник (ответвление к прибору)
- короб К1 над чистым полом (ГКЛВ под плитку)
- ○ вывод В1 (код — в ведомости привязок)
- ○ вывод Т3 (код — в ведомости привязок)
- ○ вывод К1 (код — в ведомости привязок)
- сантехприбор по расстановке (габарит модели)
- ○ стояк «Ст К1-N / Ст В1-N» (ГОСТ 21.601), Ø мм
- ○ стояк Т3 не на обмере — принят в шахте рядом со Ст В1, сверить
- линия обрыва (граница фрагмента)
- граница фрагмента на плане (Фр. N)

Профиль выпусков К1 (до врезки в стояк)

Выпуск	Прибор	Ø	L, м	i, мм/м	Δh, мм	Прокладка, мм
К1-7	С-06 унитаз подвесной	Ø110	3,60	15	54	короб 200×140
К1-2	С-02 унитаз подвесной	Ø110	0,35	20	7	над полом за приборами
К1-5	С-05 мойка кухонная	Ø50	10,10	20	202	в полу не помещается: 307 > 170; до решения
К1-6	ОБ-03 посудомоечная машина	Ø50	7,60	20	152	в полу не помещается: 257 > 170; до решения
К1-1	С-01 ванна	Ø50	2,30	20	46	в полу, стяжка ≥ 151
К1-3	С-03 умывальник	Ø40	2,65	30	80	короб 150×110
К1-8	С-07 умывальник	Ø40	2,50	30	75	короб 150×110
К1-4	ОБ-02 стиральная машина	Ø40	1,05	30	32	в полу, стяжка ≥ 127

Короб h×b: h — от чистого пола, b — от чистовой стены. Стяжка 155 мм — лист полов.

Узел ввода В1, Т3 (схема, без масштаба)

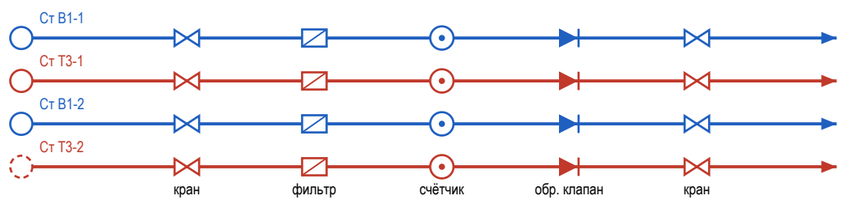

состав узла — по согласованию

⊗ Ст К1-1, Ст К1-2: ревизия на стояке — люк в коробе


Примечания

1. Трассы принципиальные, построены от стояков вдоль стен помещений; фактическое положение фиксируется исполнительной схемой с привязками (фото с рулеткой) до закрытия.
2. Уклон К1 не менее 1/d и не более 150 мм/м (СП 30.13330.2020, п. 19.1), приняты практические уклоны; поворот — двумя отводами 45°, ревизия после поворота, доступ сохранить. Стояк К1 в коробе — звукоизоляция стояка в коробе, без жёсткого контакта короба с трубой.
3. Решение по К1: стяжка 155 мм не укрывает трубы (нужно Ø + Δh + 45 мм) — выпуски идут над чистым полом вдоль стен: К1-2 — за приборами и в раме инсталляции; К1-7, К1-3, К1-8 — в коробе ГКЛВ под плитку (размеры в профиле). Короба — на развёртках; отметку низа врезки в стояк замерить до черновых работ.
4. К1-5 (С-05 мойка кухонная, выпуск в пол): Δh 202 + Ø50 + 45 = 307 мм > пирога 170 мм — в стяжке не помещается, в короб не уходит: подиум или подъём пола на 140 мм или прибор ближе к стояку — решение заказчика; до решения не выполнять.
5. К1-6 (ОБ-03 посудомоечная машина, выпуск в пол): Δh 152 + Ø50 + 45 = 257 мм > пирога 170 мм — в стяжке не помещается, в короб не уходит: подиум или подъём пола на 90 мм или прибор ближе к стояку — решение заказчика; до решения не выполнять.
6. Состав узла ввода В1, Т3 — по согласованию: на схеме типовой узел — кран шаровой, фильтр, счётчик, обратный клапан, кран; состав и места не определены (записи реестра нет). Доступ к арматуре — через люк не меньше 300×400. Водопровод — в штробе стен или в коробах; трубы испытать давлением до закрытия (акт скрытых работ).
7. Расчёт систем, диаметры магистралей и подбор оборудования выполняет проектная организация; врезка и перенос стояков — по согласованию с управляющей организацией. Арматуру и привязки сверить по паспортам приборов.
8. Ведомость выводов (код, прибор, высота, привязка) — лист 39; на схеме — только коды.
9. Ст Т3-2 на обмере не показаны: приняты рядом с Ст В1-2 (в МКД стоят группой); положение сверить на объекте до разводки.
10. Штриховая линия чистовой грани стены прерывается на длине полотна открытой двери, лежащего вдоль грани (линии не должны сливаться при печати); положение грани — по размерам, а не по штриху.

	Лист	№ док.	Подпись	Дата	Проект: Четырёхкомнатная квартира			
Дизайнер	Кырлан А.С.			14.11.26	Схема разводки водопровода и канализации	Стадия	Лист	Листов
Проверил						П	40	147
Н. контр.								
Утв.								

выпуск 14.11.2026 № e7147312ff · стр. 40 из 147

Схема В1 (М 1:50)

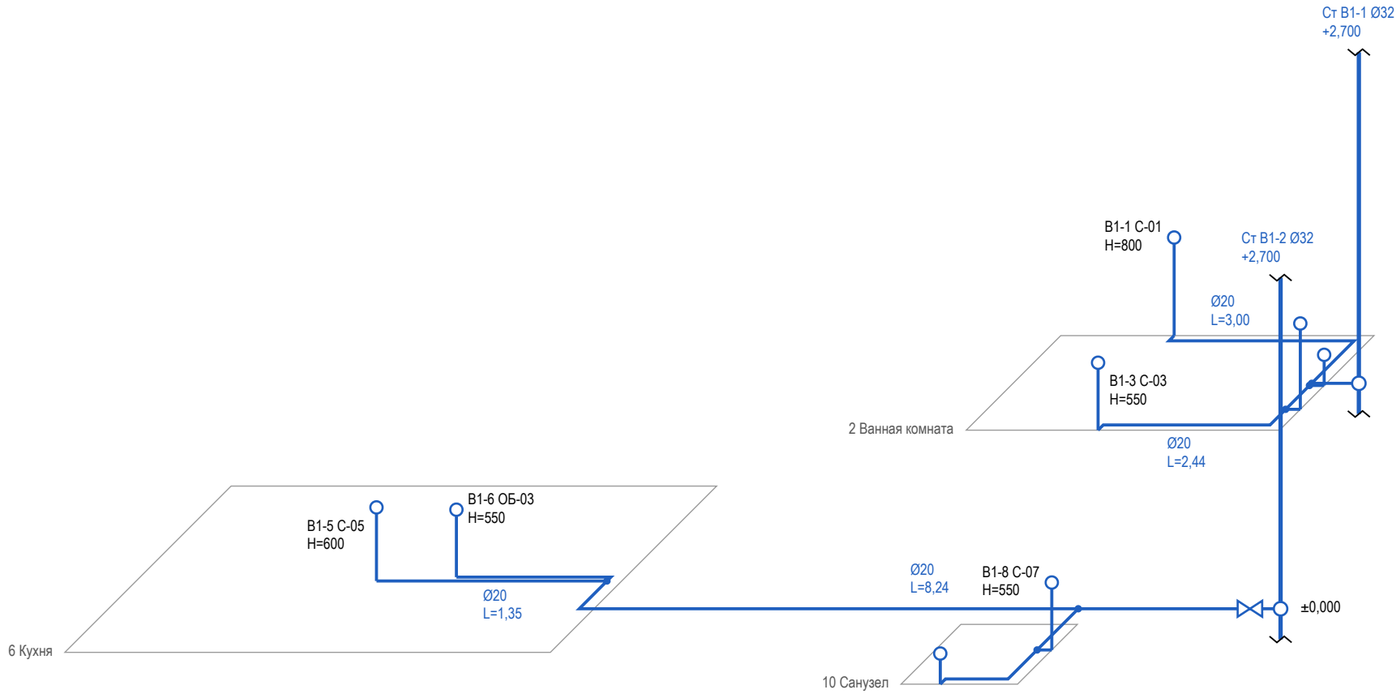

Ведомость выводов В1

Код	Прибор	H, мм	Ø, мм	Трасса, м
В1-5	С-05 мойка кухонная	600	20	8,24
В1-6	ОБ-03 посудомоечная машина	550	20	1,35
В1-7	С-06 унитаз подвесной	250	20	2,25
В1-1	С-01 ванна	800	20	3,00
В1-3	С-03 умывальник	550	20	2,44
В1-8	С-07 умывальник	550	20	0,12
В1-4	ОБ-02 стиральная машина	700	20	0,12
В1-2	С-02 унитаз подвесной	250	20	0,12

Условные обозначения


- В1 — водопровод хозяйственно-питьевой (ХВС), PP-R Ø20
- вывод В1 (код — в ведомости привязок)
- стояк «Ст К1-N / Ст В1-N» (ГОСТ 21.601), Ø мм
- стояк в плане (на отметке пола); вертикаль — стояк по высоте, разрыв — перекрытие
- тройник (ответвление к прибору)
- кран шаровой

Примечания

1. Схема В1 построена по тем же трассам, что план разводки: положение в плане сохранено, глубина — в масштабе ×0,5. Трассы принципиальные; фактическое положение фиксируется исполнительной схемой до закрытия.
2. Высоты H — от чистого пола помещения, мм. Отметка прокладки магистрали В1 (в стяжке, в стене или по полу) в данных не задана: участки показаны на уровне пола условно (записи реестра нет).
3. Узел ввода В1 (кран, фильтр, счётчик, обратный клапан, кран) — на схеме разводки; состав узла ввода — по согласованию. Кран шаровой — на первом участке от стояка.
4. Трубы испытать давлением до закрытия (акт скрытых работ, опрессовка по СП 73.13330.2016).
5. Диаметры, высоты выводов и места кранов — по паспортам выбранных приборов и расчёту проектной организации.
6. Расчёт систем, диаметры магистралей и подбор оборудования выполняет проектная организация.

	Лист	№ док.	Подпись	Дата	Проект: Четырёхкомнатная квартира			М 1:50
Дизайнер	Кырлан А.С.			14.11.26	Аксонометрическая схема В1 (холодное водоснабжение)	Стадия	Лист	Листов
Проверил						П	41	147
Н. контр.								
Утв.								

Схема Т3 (М 1:50)

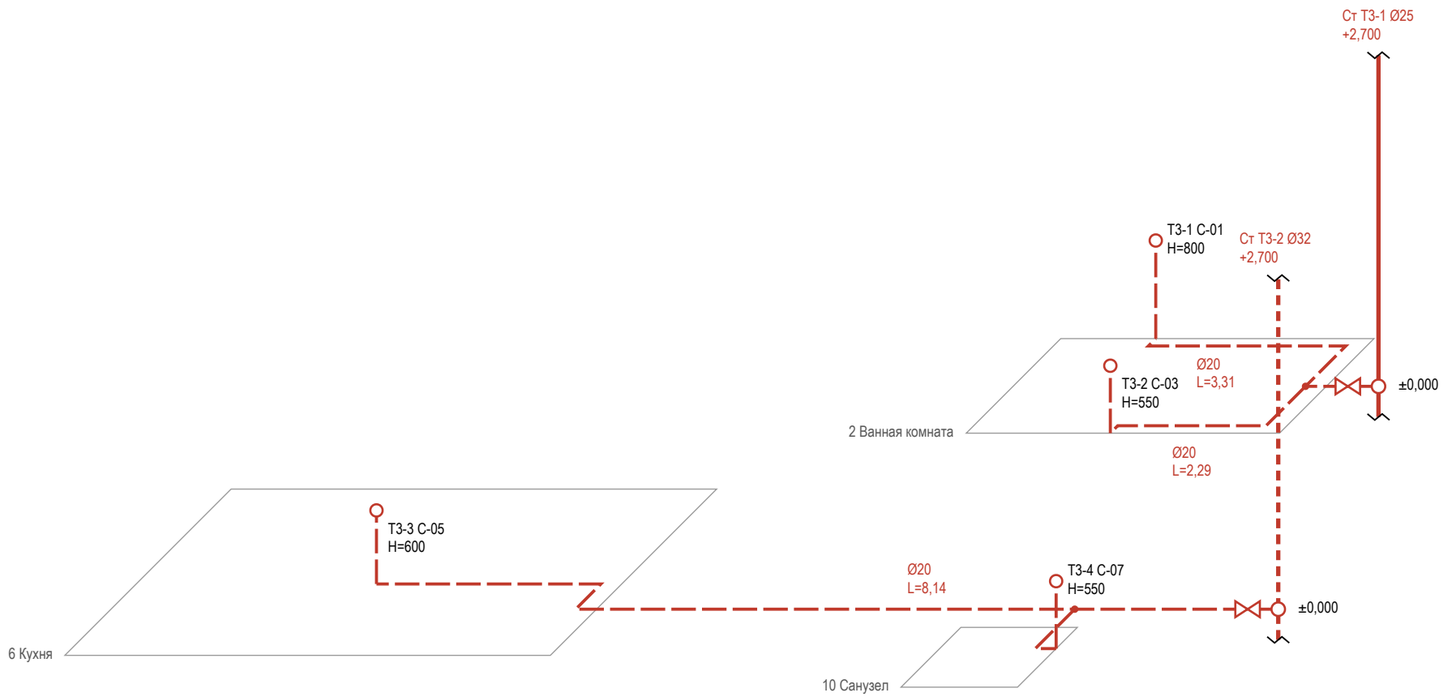

Ведомость выводов Т3

Код	Прибор	H, мм	Ø, мм	Трасса, м
Т3-3	С-05 мойка кухонная	600	20	8,14
Т3-1	С-01 ванна	800	20	3,31
Т3-2	С-03 умывальник	550	20	2,29
Т3-4	С-07 умывальник	550	20	1,08

Условные обозначения

- Т3 — горячее водоснабжение, подача (ГВС), PP-R Ø20
- вывод Т3 (код — в ведомости привязок)
- стояк «Ст К1-N / Ст В1-N» (ГОСТ 21.601), Ø мм
- стояк в плане (на отметке пола); вертикаль — стояк по высоте, разрыв — перекрытие
- тройник (ответвление к прибору)
- кран шаровой
- стояк Т3 не на обмере — принят в шахте рядом со Ст В1, сверить

Примечания

1. Схема Т3 построена по тем же трассам, что план разводки: положение в плане сохранено, глубина — в масштабе ×0,5. Трассы принципиальные; фактическое положение фиксируется исполнительной схемой до закрытия.
2. Высоты H — от чистого пола помещения, мм. Отметка прокладки магистрали Т3 (в стяжке, в стене или по полу) в данных не задана: участки показаны на уровне пола условно (записи реестра нет).
3. Узел ввода Т3 (кран, фильтр, счётчик, обратный клапан, кран) — на схеме разводки; состав узла ввода — по согласованию. Кран шаровой — на первом участке от стояка.
4. Циркуляция ГВС в данных не задана — циркуляционного трубопровода на схеме нет (записи реестра нет).
5. Ст Т3-2 на обмере не показаны: приняты рядом с Ст В1-2 (в МКД стоят группой); положение сверить на объекте до разводки.
6. Трубы испытать давлением до закрытия (акт скрытых работ, опрессовка по СП 73.13330.2016).
7. Диаметры, высоты выводов и места кранов — по паспортам выбранных приборов и расчёту проектной организации.
8. Расчёт систем, диаметры магистралей и подбор оборудования выполняет проектная организация.


	Лист	№ док.	Подпись	Дата
Дизайнер	Кырлан А.С.			14.11.26
Проверил				
Н. контр.				
Утв.				

Проект: Четырёхкомнатная квартира — **М 1:50**

Аксонометрическая схема Т3 (горячее водоснабжение)

Стадия	Лист	Листов
П	42	147

Схема К1 (М 1:50)

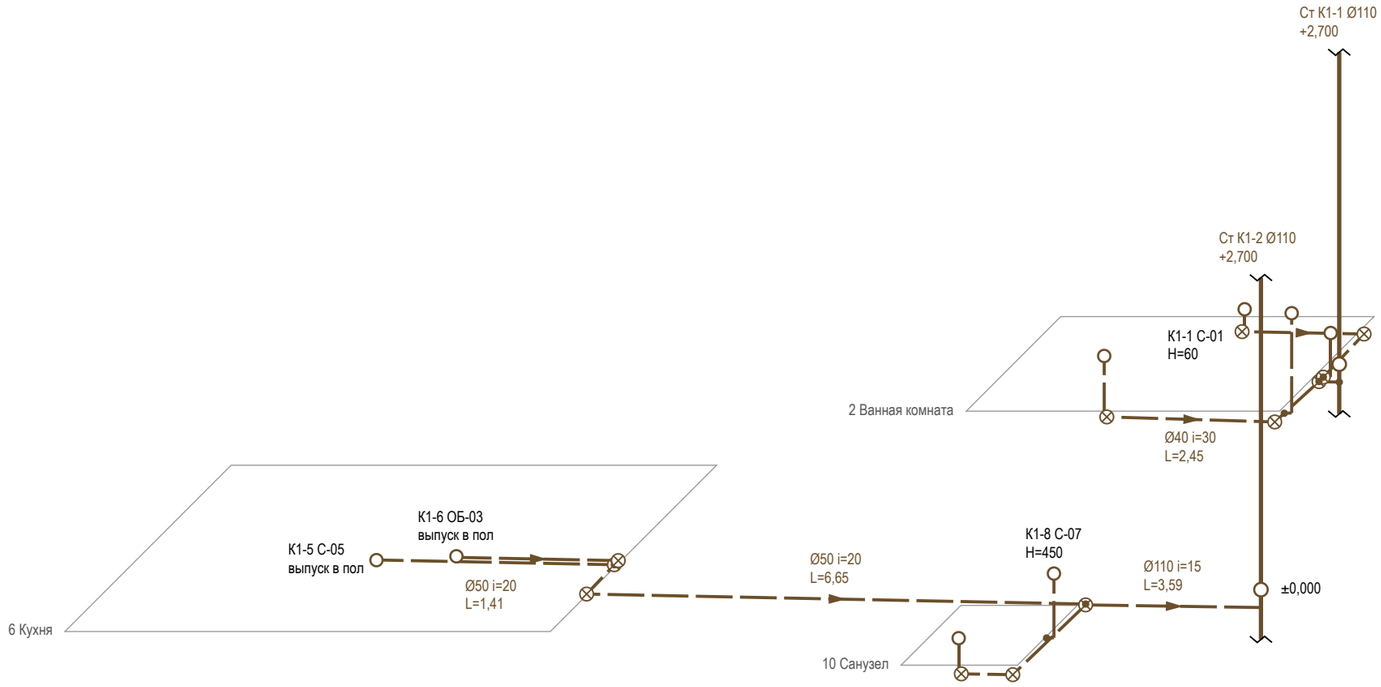

Ведомость выводов К1

Код	Прибор	H, мм	Ø, i	Трасса, м
К1-7	С-06 унитаз подвесной	220	110 i=15	3,59
К1-2	С-02 унитаз подвесной	220	110 i=20	0,33
К1-5	С-05 мойка кухонная	в пол	50 i=20	6,65
К1-6	ОБ-03 посудомоечная машина	в пол	50 i=20	1,41
К1-1	С-01 ванна	60	50 i=20	2,00
К1-3	С-03 умывальник	450	40 i=30	2,45
К1-8	С-07 умывальник	450	40 i=30	0,06
К1-4	ОБ-02 стиральная машина	700	40 i=30	0,06

Условные обозначения


- К1 — канализация бытовая
- вывод К1 (код — в ведомости привязок)
- стояк «Ст К1-N / Ст В1-N» (ГОСТ 21.601), Ø мм
- стояк в плане (на отметке пола); вертикаль — стояк по высоте, разрыв — перекрытие
- направление уклона К1 / пола: Ø, мм на 1 м
- ревизия (прочистка) К1 — доступ сохранить
- тройник (ответвление к прибору)

Примечания


1. Схема К1 построена по тем же трассам, что план разводки: положение в плане сохранено, глубина — в масштабе ×0,5. Трассы принципиальные; фактическое положение фиксируется исполнительной схемой до закрытия.
2. Отметки — от плиты перекрытия: низ трубы у врезки в стояк — отметка из данных выпуска, к прибору труба поднимается на уклон i, мм/м (уклон не менее 1/d и не более 150 мм/м, СП 30.13330.2020, п. 19.1); чистый пол — выше плиты на стяжку (высота пирога пола). Высота выпуска прибора H — от чистого пола.
3. Ревизия — на повороте и в начале участка; стояк К1 в коробе с люком — звукоизоляция стояка в коробе; поворот — двумя отводами 45°.
4. Трубы испытать давлением до закрытия (акт скрытых работ, опрессовка по СП 73.13330.2016).
5. Диаметры, высоты выводов и места кранов — по паспортам выбранных приборов и расчёту проектной организации.
6. Расчёт систем, диаметры магистралей и подбор оборудования выполняет проектная организация.

	Лист	№ док.	Подпись	Дата	Проект: Четырёхкомнатная квартира			M 1:50
Дизайнер	Кырлан А.С.			14.11.26	Аксонометрическая схема К1 (канализация)	Стадия	Лист	Листов
Проверил						П	43	147
Н. контр.								
Утв.								


Стена А (М 1:25)

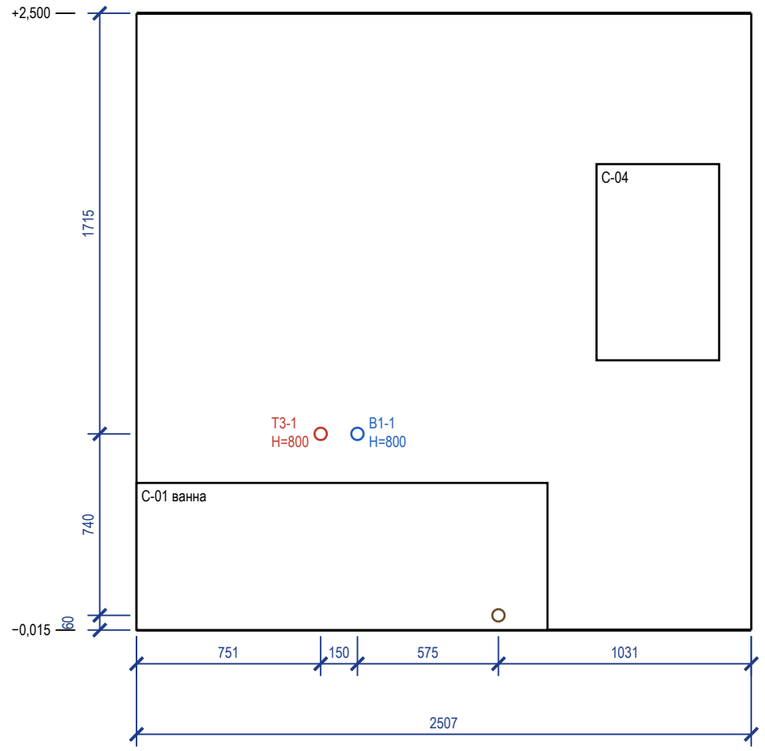

Стена Б (М 1:25)

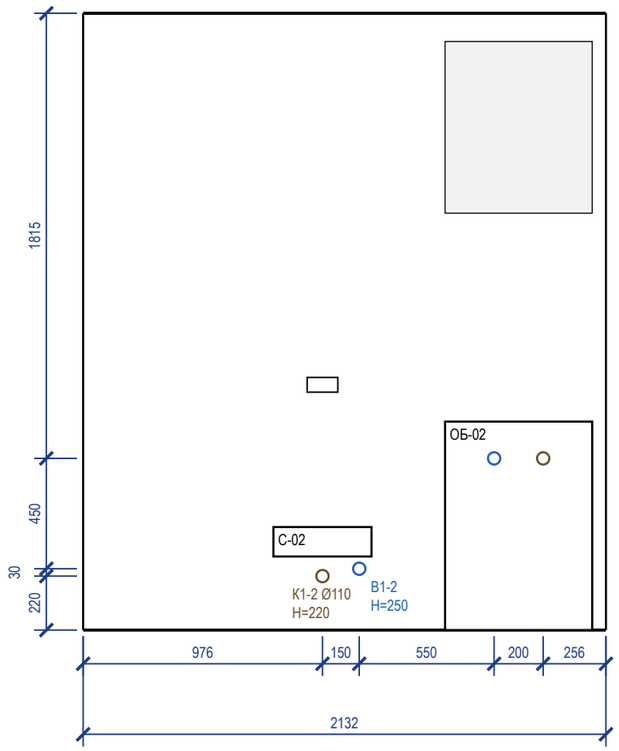

Стена В (М 1:25)

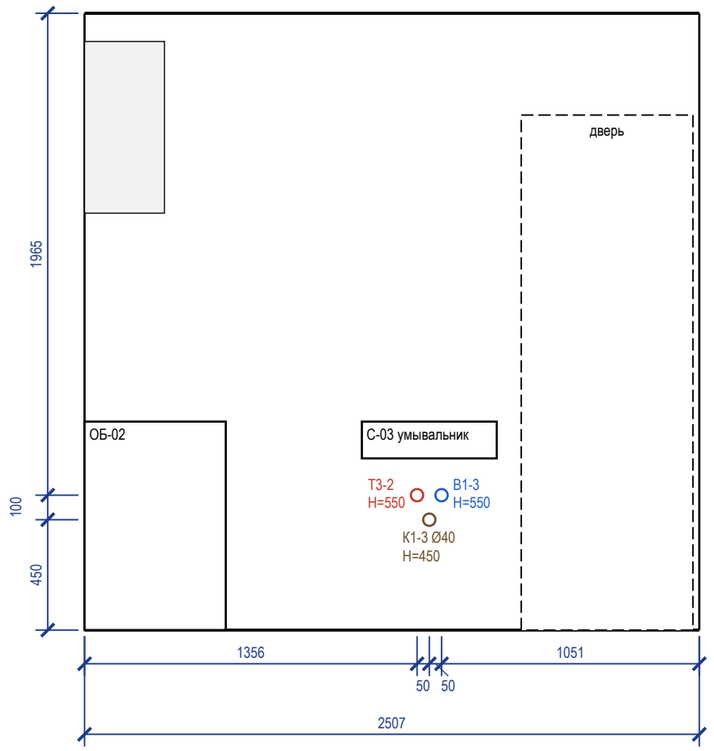

Ведомость привязок выводов (от чистого пола и угла)

Код	Прибор	Ø	H, мм	Привязка, мм
В1-1	С-01 ванна	½"	800	ст. А: 901 от лев. угла
Т3-1	С-01 ванна	½"	800	ст. А: 751 от лев. угла
К1-1	С-01 ванна	Ø50	60	ст. А: 1476 от лев. угла
В1-2	С-02 унитаз подвесной	½"	250	ст. Б: 1126 от лев. угла
К1-2	С-02 унитаз подвесной	Ø110	220	ст. Б: 976 от лев. угла
В1-4	ОБ-02 стиральная машина	½"	700	ст. Б: 1676 от лев. угла
К1-4	ОБ-02 стиральная машина	Ø40	700	ст. Б: 1876 от лев. угла
В1-3	С-03 умывальник	½"	550	ст. В: 1456 от лев. угла
Т3-2	С-03 умывальник	½"	550	ст. В: 1356 от лев. угла
К1-3	С-03 умывальник	Ø40	450	ст. В: 1406 от лев. угла

Условные обозначения


- вывод В1 (код — в ведомости привязок)
- вывод Т3 (код — в ведомости привязок)
- вывод К1 (код — в ведомости привязок)
- сантехприбор по расстановке (габарит модели)
- дверной проём; окно — сплошной контур
- кнопка смыва инсталляции (Н — по данным прибора)

Примечания


1. Габариты и высоты приборов, межосевые смесителей и места кранов — по паспортам выбранных приборов, сверяются до разметки стен.
2. Высоты Н — от чистого пола помещения, мм; отметка чистого пола и потолка — у левого края вида (от ±0,000 объекта). Привязки — от левого чистового угла вида (облицовка стен вычтена), как на развёртках стен.
3. Кнопка смыва С-02 — Н=1000 (по данным прибора).
4. Ревизионные люки (ревизия К1 в коробе за стиральной машиной 300×400): место в стене на развёртке не задано (записи реестра нет).
5. Часть подписей выводов не уместилась у знака: коды и высоты — в ведомости привязок.
6. Стены Г: выводов В1, Т3, К1 нет — развёртка не строится (иначе лист-продолжение); приборы и проёмы этих стен — на плане выводов и развёртках стен чертёжника.
7. Расчёт систем водоснабжения и канализации и подбор оборудования выполняет проектная организация; лист задаёт места и высоты выводов.

	Лист	№ док.	Подпись	Дата	Проект: Четырёхкомнатная квартира			М 1:25
Дизайнер	Кырлан А.С.			14.11.26	Развёртки мокрых зон: выводы ВК. Ванная комната	Стадия	Лист	Листов
Проверил						П	44	147
Н. контр.								
Утв.								

Стена Б (М 1:20)

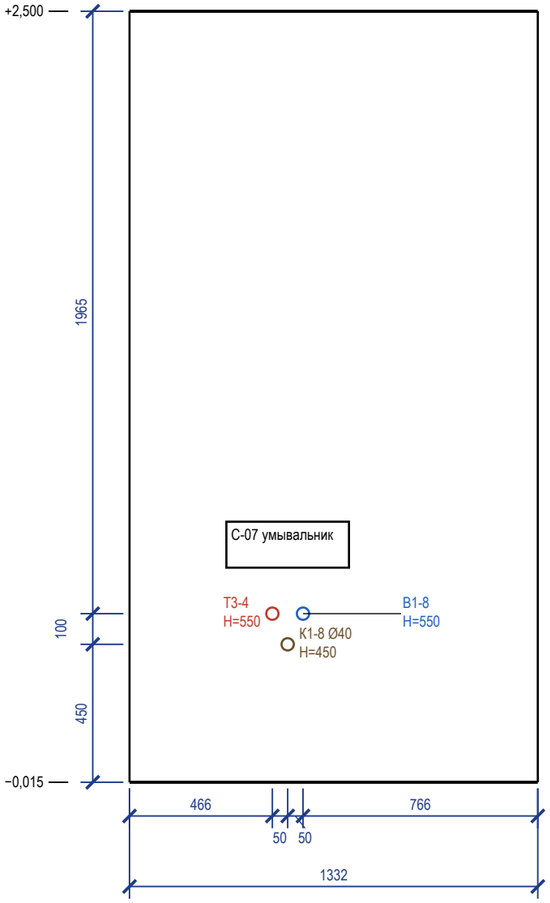

Стена В (М 1:20)

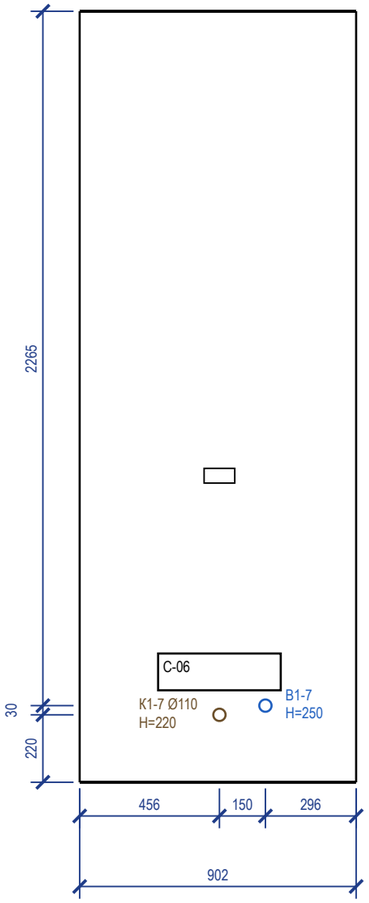

Ведомость привязок выводов (от чистого пола и угла)

Код	Прибор	Ø	H, мм	Привязка, мм
B1-8	C-07 умывальник	½"	550	ст. Б: 566 от лев. угла
T3-4	C-07 умывальник	½"	550	ст. Б: 466 от лев. угла
K1-8	C-07 умывальник	Ø40	450	ст. Б: 516 от лев. угла
B1-7	C-06 унитаз подвесной	½"	250	ст. В: 606 от лев. угла
K1-7	C-06 унитаз подвесной	Ø110	220	ст. В: 456 от лев. угла

Условные обозначения

- вывод B1 (код — в ведомости привязок)
- вывод T3 (код — в ведомости привязок)
- вывод K1 (код — в ведомости привязок)
- сантехприбор по расстановке (габарит модели)
- дверной проём; окно — сплошной контур
- кнопка смыва инсталляции (H — по данным прибора)

Примечания

1. Габариты и высоты приборов, межосевые смесителей и места кранов — по паспортам выбранных приборов, сверяются до разметки стен.
2. Высоты H — от чистого пола помещения, мм; отметка чистого пола и потолка — у левого края вида (от ±0,000 объекта). Привязки — от левого чистового угла вида (облицовка стен вычтена), как на развёртках стен.
3. Кнопка смыва C-06 — H=1000 (по данным прибора).
4. Ревизионные люки к арматуре и ревизиям в данных не заданы: место и размер не определены (записи реестра нет).
5. Расчёт систем водоснабжения и канализации и подбор оборудования выполняет проектная организация; лист задаёт места и высоты выводов.

	Лист	№ док.	Подпись	Дата
Дизайнер	Кырлан А.С.			14.11.26
Проверил				
Н. контр.				
Утв.				

Проект: Четырёхкомнатная квартира — **М 1:20**

Развёртки мокрых зон: выводы ВК. Санузел

Стадия	Лист	Листов
П	45	147


выпуск 14.11.2026 № e7147312ff · стр. 45 из 147

Поз.	Наименование и техническая характеристика	Тип, марка, обозначение документа	Код продукции	Поставщик	Ед. изм.	Кол.	Масса 1 ед., кг	Примечание
	Санитарные приборы							
1	Ванна встраиваемая акриловая 1700×750 мм, с каркасом, экраном и отверстием слив-перелив	акриловая 1700×750, смеситель настенный термостатический		выбор заказчика	шт	1	35	С-01
2	Унитаз подвесной безободковый, с сиденьем микролифт, крепёж и звукоизолирующая прокладка	аналог		выбор заказчика	шт	2		С-02, С-06
3	Инсталляция для подвесного унитаза: рама высотой 1120 мм, бачок, клавиша смыва (ось клавиши 1050 мм от чистого пола)	аналог		выбор заказчика	шт	2		С-02, С-06; короб ГКЛВ
4	Умывальник подвесной 550×450 мм, с отверстием под смеситель и переливом	аналог		выбор заказчика	шт	1		С-03
5	Умывальник подвесной 400×200 мм, с отверстием под смеситель и переливом	аналог		выбор заказчика	шт	1		С-07
6	Мойка кухонная врезная 760×480 мм, с переливом	аналог		с кухонной мебелью	шт	1		С-05
7	Полотенцесушитель электрический, IP44, с терморегулятором	аналог		выбор заказчика	шт	1		С-04
	Смесители, сифоны и арматура приборов							
8	Смеситель для ванны настенный однорычажный, межосевое 150 мм, с душевым набором (лейка, шланг, держатель)	аналог		выбор заказчика	шт	1		С-01
9	Смеситель для умывальника однорычажный, с донным клапаном	аналог		выбор заказчика	шт	2		С-03, С-07
10	Смеситель кухонный однорычажный, высокий излив	аналог		выбор заказчика	шт	1		С-05
11	Обвязка ванны слив-перелив Ø40/50 с сифоном	аналог		выбор заказчика	шт	1		С-01
12	Сифон для умывальника бутылочный Ø32/40–50, с гофрой к выпуску	аналог		выбор заказчика	шт	2		С-03, С-07
13	Сифон для мойки Ø40/50	аналог		выбор заказчика	шт	1		С-05
14	Сифон для посудомоечной машины с обратным клапаном, на выводе слива Ø40	аналог		выбор заказчика	шт	1		ОБ-03
15	Сифон для стиральной машины встраиваемый в стену Ø50, с обратным клапаном	аналог		выбор заказчика	шт	1		ОБ-02
16	Кран угловой ½"×½" с гибкой подводкой 40 см (умывальники, мойка)	аналог		выбор заказчика	шт	6		по 2 на прибор
17	Кран шаровой угловой ½"×¾" для подключения стиральной и посудомоечной машины	аналог		выбор заказчика	шт	2		ОБ-02, ОБ-03
	Трубопроводы							
18	Труба полипропиленовая PP-R PN20 Ø20×3,4 (В1)	ГОСТ 32415-2013		выбор заказчика	м	24,5	0,17	17,6 + 4,3 + 10 %
19	Труба PP-R, армированная стекловолокном, PN20 Ø20×2,8 (Т3)	ГОСТ 32415-2013		выбор заказчика	м	19,5	0,15	14,8 + 2,5 + 10 %
20	Труба канализационная ПП Ø40 (К1)	ГОСТ 32414-2013		выбор заказчика	м	5		2,6 + 1,6 + 10 %
21	Труба канализационная ПП Ø50 (К1)	ГОСТ 32414-2013		выбор заказчика	м	12,5		10,1 + 1,0 + 10 %
22	Труба канализационная ПП Ø110 (К1)	ГОСТ 32414-2013		выбор заказчика	м	5		3,9 + 0,4 + 10 %
	Фасонные части и выводы							
23	Отвод канализационный ПП 45° Ø40	ГОСТ 32414-2013		выбор заказчика	шт	4		2 шт. на поворот
24	Отвод канализационный ПП 45° Ø50	ГОСТ 32414-2013		выбор заказчика	шт	10		2 шт. на поворот
25	Отвод канализационный ПП 45° Ø110	ГОСТ 32414-2013		выбор заказчика	шт	10		2 шт. на поворот
26	Тройник канализационный ПП 45° (врезки ветвей)	ГОСТ 32414-2013		выбор заказчика	шт	7		
27	Ревизия канализационная ПП (после поворота трассы)	ГОСТ 32414-2013		выбор заказчика	шт	6		доступ сохранить
28	Фитинги PP-R Ø20: тройники, угольники 90° (ветви и повороты В1, Т3)	ГОСТ 32415-2013		выбор заказчика	шт	28		
29	Водорозетка PP-R Ø20×½" настенная, с креплением	ГОСТ 32415-2013		выбор заказчика	шт	12		коды — лист выводов
	Узлы ввода, люки, короба							
30	Кран шаровой латунный Ду15 PN16 (отключение ввода)	аналог		выбор заказчика	шт	4		Ст В1-1, Ст Т3-1, Ст В1-2, Ст Т3-2
31	Фильтр сетчатый косой Ду15	аналог		выбор заказчика	шт	4		
32	Счётчик воды крыльчатый Ду15 (ХВ, ГВ), с поверкой	аналог		выбор заказчика	шт	4		пломба УК
33	Клапан обратный Ду15	аналог		выбор заказчика	шт	4		
34	Люк ревизионный нажимной под плитку 300×400 мм	аналог		выбор заказчика	шт	4		к стоякам и арматуре
35	Звукоизоляция стояка К1 в коробе: рулонный звукоизоляционный материал ≥ 10 мм, обмотка стояка на высоту этажа	аналог		выбор заказчика	м	5,4		Ст К1-1, Ст К1-2
36	Короб К1 над полом: профиль ПН/ПС, ГКЛВ 12,5 мм под плитку	аналог		выбор заказчика	м	5,8		сечение — лист разводки

Примечания

1. Форма 1 ГОСТ 21.110-2013, ширины граф изменены по п. 4.1. «Аналог» — аналог по характеристикам: модели внести до черновых работ, привязки выводов сверить по паспортам.
2. Бытовая техника не входит (показана арматура подключения), мойка — в комплекте кухни (марка — модуля кухни, как у столяра). Длины труб — трасса листа разводки + подъёмы + 10 %.
3. Стояк К1 в коробе — звукоизоляция стояка в коробе без жёсткого контакта короба с трубой.
4. Расчёт систем водоснабжения и канализации, диаметры магистралей и подбор оборудования выполняет проектная организация.

	Лист	№ док.	Подпись	Дата	Проект: Четырёхкомнатная квартира			
Дизайнер	Кырлан А.С.			14.11.26				
Проверил					Спецификация сантехнического оборудования	Стадия	Лист	Листов
Н. контр.						П	46	147
Утв.								

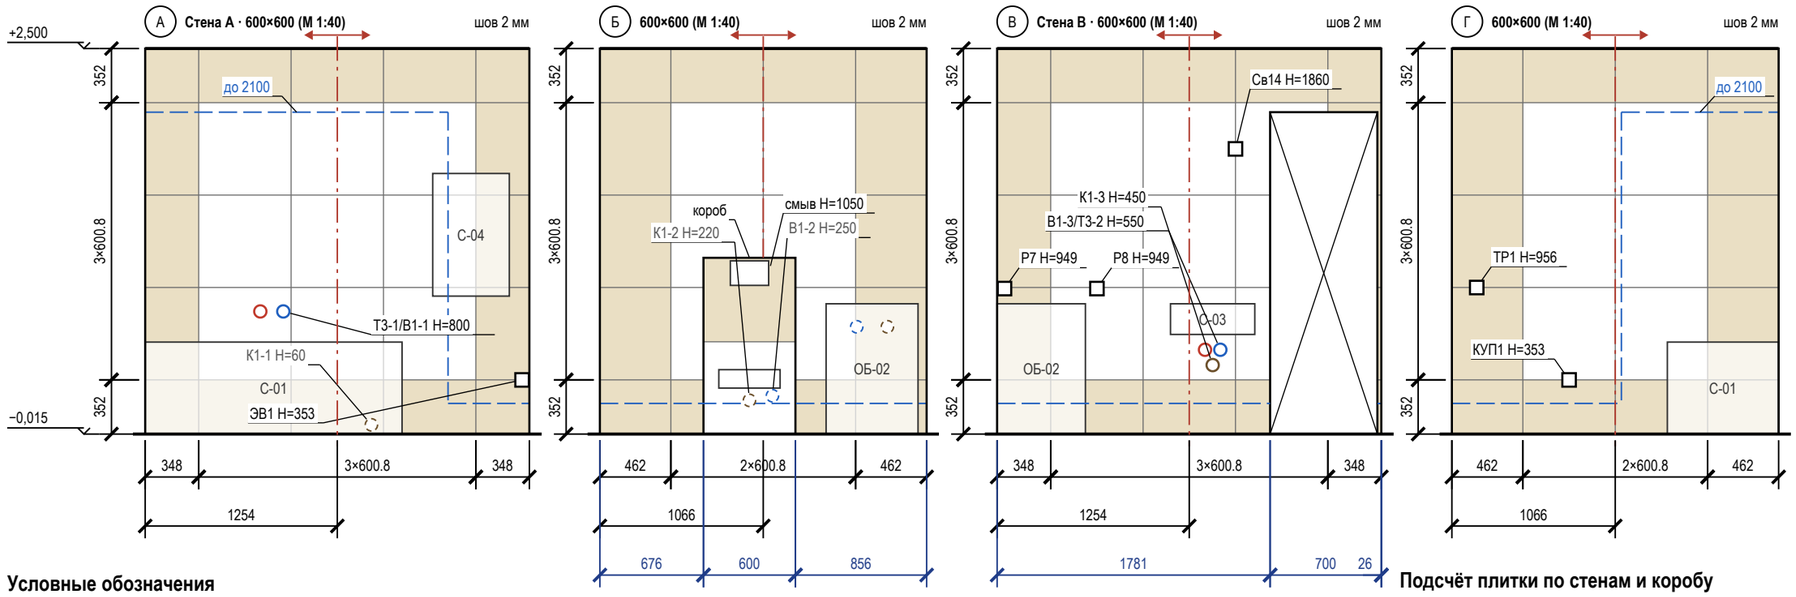

Условные обозначения

- плитка целая; тонкая линия — шов
- плитка с подрезкой (размер — на цепочке)
- ось старта; стрелки — направление укладки
- верх гидроизоляции: 200 от ЧП, в мокрой зоне — «до …»
- проём — не облицовывается
- сантехприбор: габарит, высота по практике
- короб инсталляции, в нём кнопка смыва 250×160
- вывод В1 (код — в ведомости привязок)
- вывод Т3 (код — в ведомости привязок)
- вывод К1 (код — в ведомости привязок)
- вывод за прибором / в коробе (не на сетке)
- электроточка: марка и Н — по листам ЭОМ
- отметка уровня, м: ±0,000 — чистый пол жилых помещений
- низ потолка; серая полоса — стена без плитки
- (А) обозначение стены А–Г (как на развёртках)

Примечания


1. Вид изнутри, стены по часовой стрелке А → Г. Высоты — от чистого пола (−0,015), отметки — от ±0,000. Раскладка от чистовых размеров (штукатурка 10 + клей 5 + плитка 9 мм), подрезки чистые; старт — от оси стены, ряды от середины (две подрезки).
2. Облицовка до потолка (+2,500).
3. Открытые выводы и электроточки — на шве или в центре плитки (допуск 10 мм; плитка от 900 мм по высоте — на шве или не ближе 60 мм к нему).
4. Выводы ВК стоят по оси прибора и с прибором не двигаются — привязки по «Плану выводов сантехники» без сдвига; вне сетки (Т3-1/В1-1, В1-3/Т3-2, К1-3) отверстие в плитке коронкой по той же привязке, плитку не сдвигать.
5. За приборами и в коробе (К1-1, В1-2, К1-2, В1-4, К1-4) — штриховым кольцом.
6. Гидроизоляция: 200 мм от ЧП по периметру; над ванной — до 2100 и 300 мм за борт (СП 29.13330.2011, п. 7.2 — на высоту замачивания); углы — лентой; акт скрытых работ, пролив.
7. Короб 600×1150×230: лицо 600 мм от оси кнопки смыва, боковины, полка; углы — запил 45° или профиль; за коробом плитку не кладут.
8. Наружные углы: ст. Б: 2 — запил 45°; ст. В: 2 — профиль.
9. Люки: Л1 (ст. Б, 600×600, нажимной) — кромки дверцы по швам сетки.

Подсчёт плитки по стенам и коробу

Поверхность	L × H, мм	S, м²	Целых	Подр.	С запасом	Подрезки: край / верх, мм
стена А	2507 × 2515	6,43	9	16	28	348 / 348; 352
стена Б	2132 × 2515	4,79	2	18	22	462 / 462; 352
короб (ст. Б)	600×1150×230	1,36	1	6	8	лицо 600; бок. 230
стена В	2507 × 2515	4,96	6	19	28	348 / 348; 352
стена Г	2132 × 2515	5,48	6	14	22	462 / 462; 352
Итого		**23,01**	**24**	**73**	**108**	

выпуск 14.11.2026 № e7147312ff · стр. 47 из 147

	Лист	№ док.	Подпись	Дата	Проект: Четырёхкомнатная квартира			М 1:40
Дизайнер	Кырлан А.С.			14.11.26				
Проверил					Раскладка плитки. Ванная комната. Развёртки стен	Стадия	Лист	Листов
Н. контр.						П	47	147
Утв.								

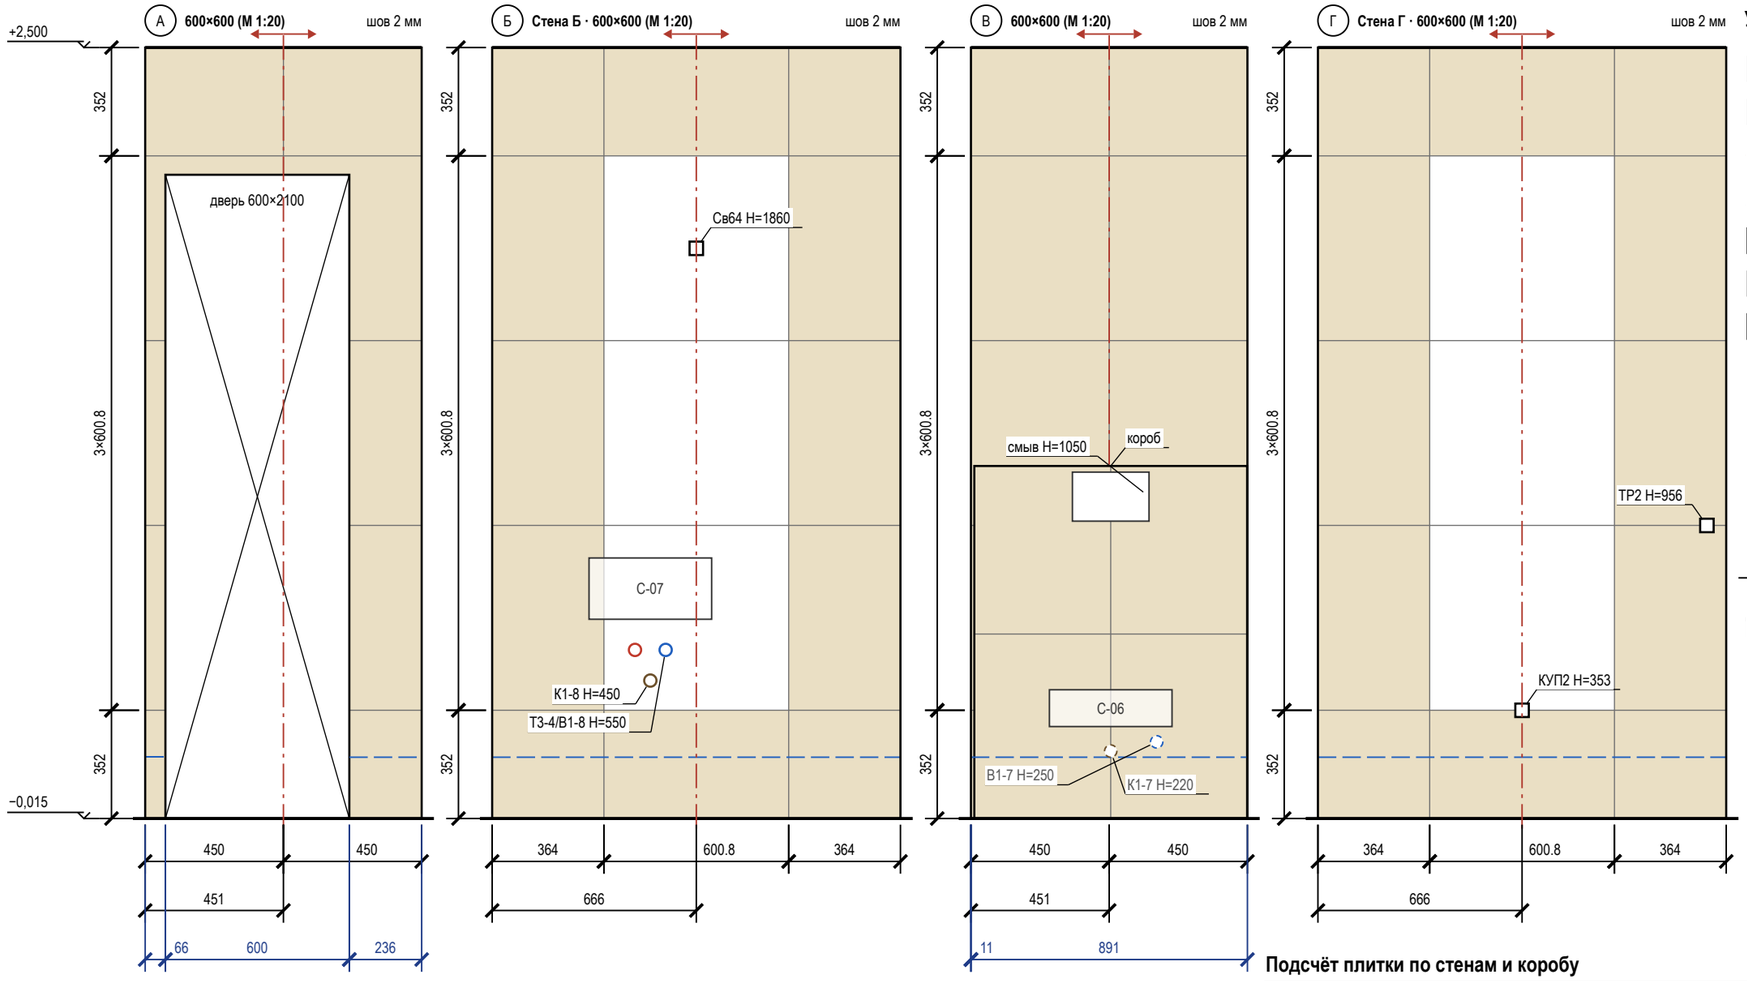

Условные обозначения

- плитка целая; тонкая линия — шов
- плитка с подрезкой (размер — на цепочке)
- ось старта; стрелки — направление укладки
- верх гидроизоляции: 200 от ЧП, в мокрой зоне — «до …»
- проём — не облицовывается
- сантехприбор: габарит, высота по практике
- короб инсталляции, в нём кнопка смыва 250×160
- вывод В1 (код — в ведомости привязок)
- вывод Т3 (код — в ведомости привязок)
- вывод К1 (код — в ведомости привязок)
- вывод за прибором / в коробе (не на сетке)
- электроточка: марка и Н — по листам ЭОМ
- отметка уровня, м: ±0,000 — чистый пол жилых помещений
- низ потолка; серая полоса — стена без плитки
- (А) обозначение стены А–Г (как на развёртках)

Примечания

1. Вид изнутри, стены по часовой стрелке А → Г. Высоты — от чистого пола (−0,015), отметки — от ±0,000. Раскладка от чистовых размеров (штукатурка 10 + клей 5 + плитка 9 мм), подрезки чистые; старт — от оси стены, ряды от середины (две подрезки).
2. Облицовка до потолка (+2,500).
3. Открытые выводы и электроточки — на шве или в центре плитки (допуск 10 мм; плитка от 900 мм по высоте — на шве или не ближе 60 мм к нему).
4. Выводы ВК стоят по оси прибора и с прибором не двигаются — привязки по «Плану выводов сантехники» без сдвига; вне сетки (Т3-4/В1-8, К1-8) — отверстие в плитке коронкой по той же привязке, плитку не сдвигать.
5. За приборами и в коробе (В1-7, К1-7) — штриховым кольцом.
6. Гидроизоляция: 200 мм от ЧП по периметру; углы — лентой; акт скрытых работ, пролив.
7. Короб 890×1150×230: лицо 444 / 444 мм от оси кнопки смыва, боковины, полка; углы — запил 45° или профиль; за коробом плитку не кладут.
8. Между коробом и углом полоса 11 мм — довести короб до угла.
9. Наружные углы: ст. А: 2 — профиль.

Подсчёт плитки по стенам и коробу

Поверхность	L × H, мм	S, м²	Целых	Подр.	С запасом	Подрезки: край / верх, мм
стена А	902 × 2515	1,13	0	10	11	450 / 450; 352
стена Б	1332 × 2515	3,47	3	12	17	364 / 364; 352
стена В	902 × 2515	1,37	0	10	11	450 / 450; 352
короб (ст. В)	890×1150×230	1,76	0	10	11	лицо 444 / 444; бок. 230
стена Г	1332 × 2515	3,47	3	12	17	364 / 364; 352
Итого		**11,19**	**6**	**54**	**67**	


	Лист	№ док.	Подпись	Дата
Дизайнер	Кырлан А.С.			14.11.26
Проверил				
Н. контр.				
Утв.				

Проект: Четырёхкомнатная квартира — **М 1:20**

Раскладка плитки. Санузел. Развёртки стен

Стадия	Лист	Листов
П	48	147

выпуск 14.11.2026 № e7147312ff · стр. 48 из 147

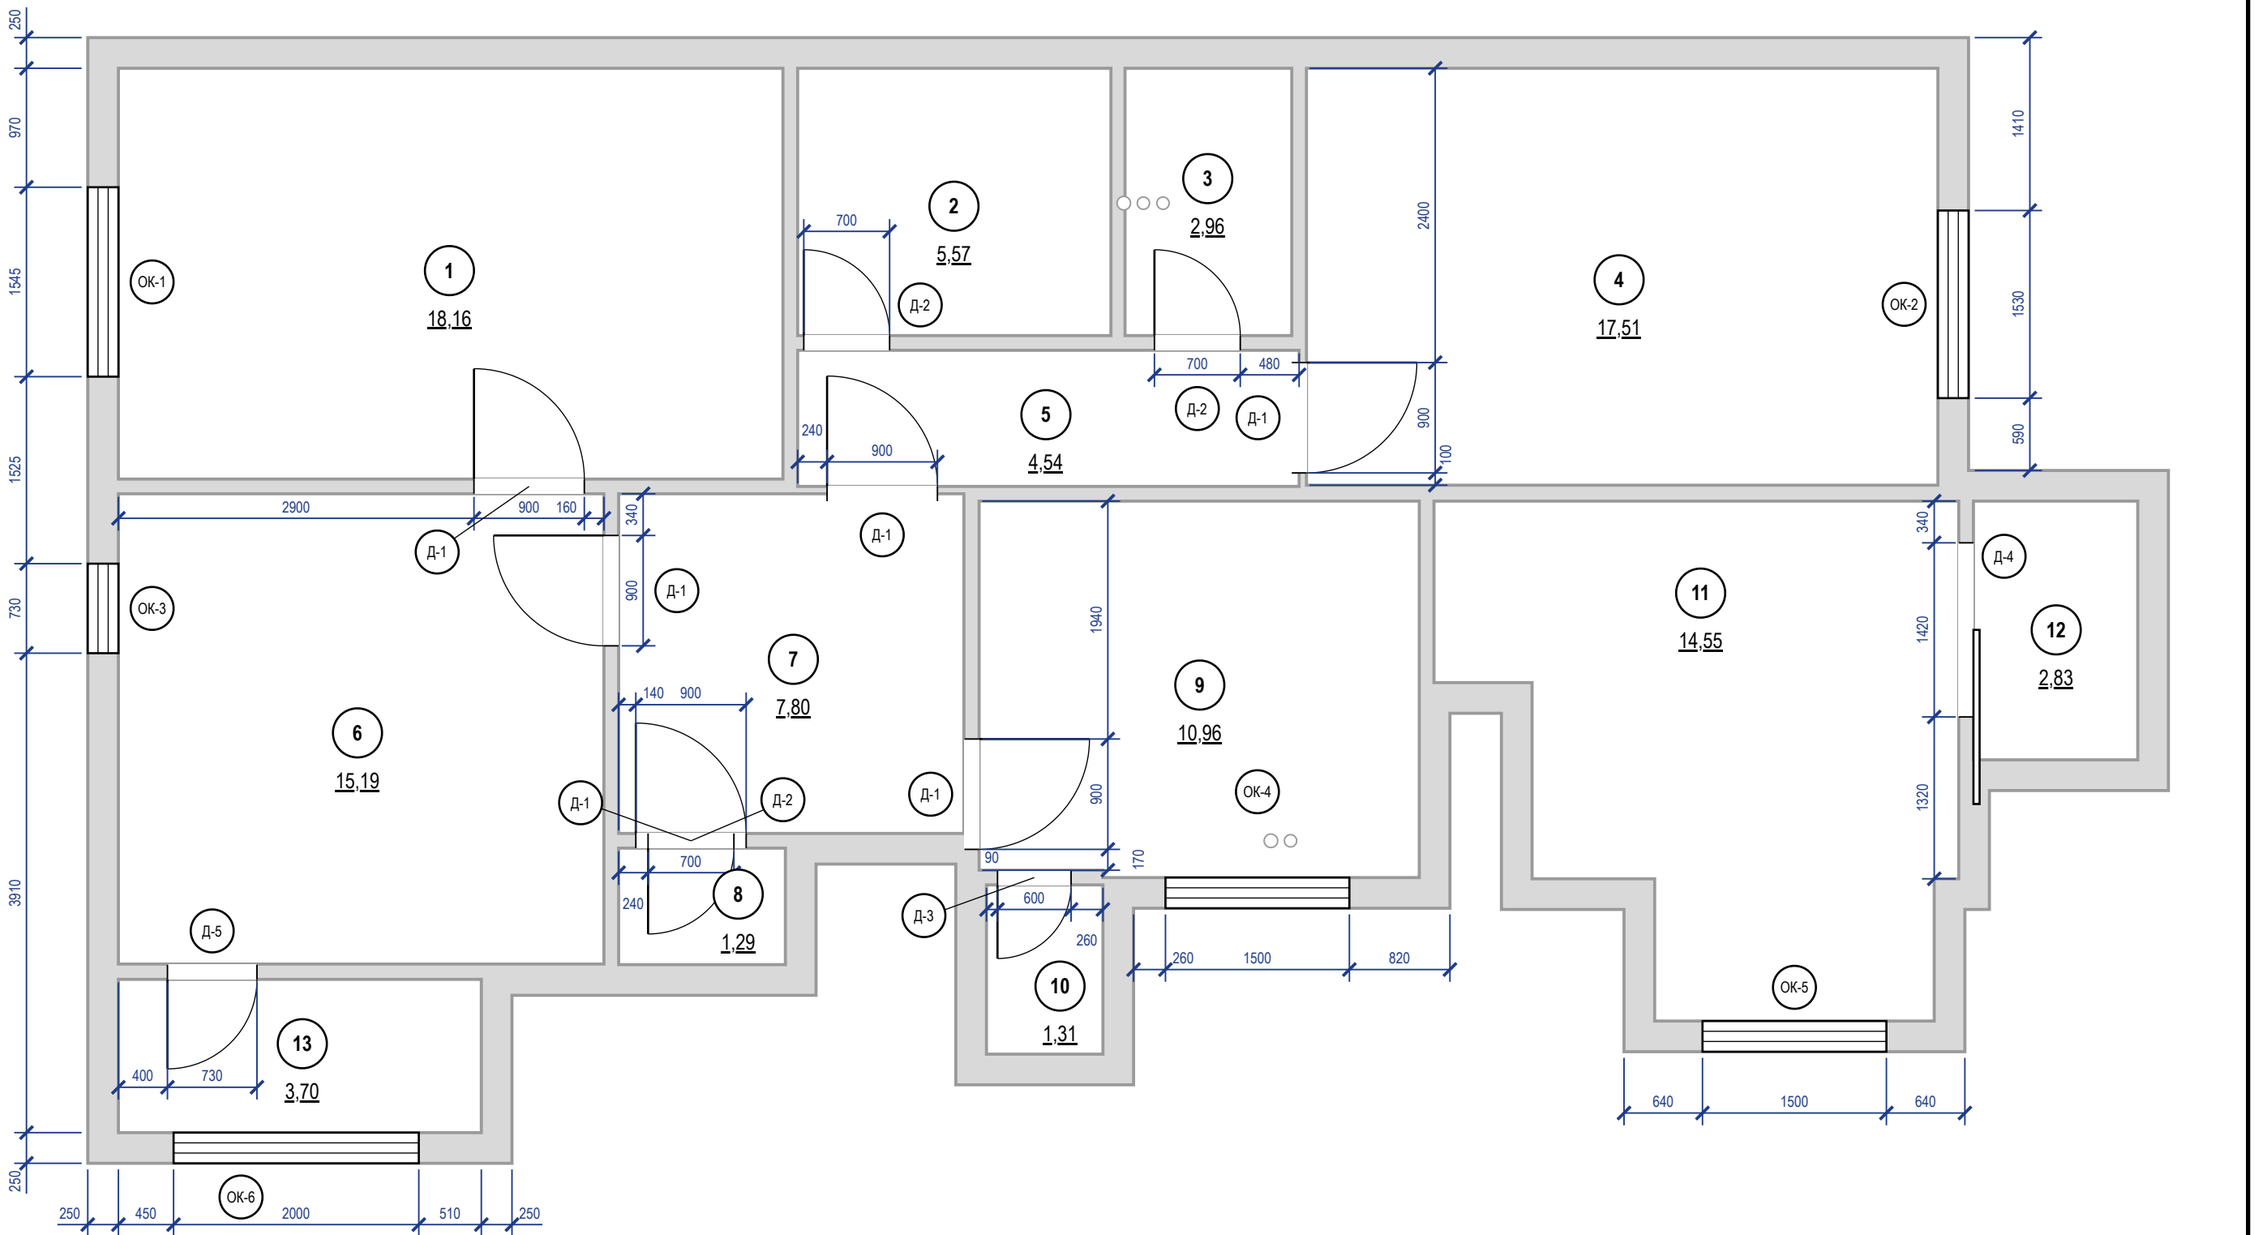

Примечания

1. Размеры проёмов и привязки — в миллиметрах от чистых граней стен до отделки; привязка — от угла того помещения, со стороны которого стоит размер. Размер проёма — ширина × высота от чистого пола 0,000. Размеры на плане — проёмов, не полотен: полотно — в ведомости, коробка — по системе.
2. Марки в кружках — типы заполнения проёмов (ГОСТ 21.501-2018, п. 5.3.2); одна марка — один типоразмер; количество сверено с планом.
3. Размеры проёмов и привязки сняты со скана плана заказчика и на объекте не замерены (обмерный план — лист 22).
4. Экспликация помещений — лист 22; в марках помещений — номер и площадь, м².
5. Ведомость проёмов — лист 50: заполнение, открывание полотен, заказ и порядок монтажа блоков.
6. Привязка проёма к углу помещения меньше 1 мм на листе, размер на плане не показан: Д-2 — 50 мм.

	Лист	№ док.	Подпись	Дата
Дизайнер	Кырлан А.С.			14.11.26
Проверил				
Н. контр.				
Утв.				

Проект: Четырёхкомнатная квартира — **М 1:50**

План размещения дверей

Стадия	Лист	Листов
П	49	147

выпуск 14.11.2026 № e7147312ff · стр. 49 из 147


Ведомость заполнения проёмов

Марка	Наименование, обозначение	Проём ш×в, мм	Полотно (расч.)	Кол.	Откр.	Отделка полотна	Фурнитура	Прим.
Д-1	Блок дверной внутренний, ГОСТ 475-2016	900×2100	800×2000	6	П, П, П, Л, П, П		петли, ручка с защёлкой	пом. 5; б/п
Д-2	Блок дверной внутренний, ГОСТ 475-2016	700×2100	600×2000	3	П, П, Л		петли, ручка с защёлкой, фиксатор WC	пом. 2; порог 15
Д-3	Блок дверной внутренний, ГОСТ 475-2016	600×2100	не задано (записи реестра нет)	1	Л		петли, ручка с защёлкой, фиксатор WC	порог 15
Д-4	Дверь раздвижная, ГОСТ 475-2016	1420×2100	не задано (записи реестра нет)	1			раздвижная система, ручки-купе	пом. 12; б/п
Д-5	Блок дверной внутренний, ГОСТ 475-2016	730×2100	не задано (записи реестра нет)	1	Л		петли, ручка с защёлкой	порог 30
ОК-1	Блок оконный, ГОСТ 23166-2021	1545×1600		1				низ 800
ОК-2	Блок оконный, ГОСТ 23166-2021	1530×1600		1				низ 800
ОК-3	Блок оконный, ГОСТ 23166-2021	730×1600		1				низ 800
ОК-4	Блок оконный, ГОСТ 23166-2021	1500×1600		1				пом. 9; низ 800
ОК-5	Блок оконный, ГОСТ 23166-2021	1500×1600		1				пом. 11; низ 900
ОК-6	Блок оконный, ГОСТ 23166-2021	2000×1700		1				низ 900

Примечания

1. Марки проёмов — те же, что на плане размещения дверей (лист 49); привязки проёмов — там же.
2. Открывание: Л — петли слева, П — справа, если смотреть со стороны, куда открывается полотно (на себя).
3. Дверные блоки обычного монтажа (Д-1…Д-5) заказывать после чистовой стяжки и штукатурки, проёмы перемерить; монтажный зазор коробки 10–15 мм на сторону, откос от угла помещения до коробки — не менее 50 мм.
4. Полотно «расч.» — по проёму с запасом по каталогам, заказ — по таблице проёмов модели; Д-1, Д-2: проём 2100, а под полотно 2000 по каталогам нужен 2040–2080, под 2100 2140–2180: высоту проёма — по модели; Д-3: проём 600×2100 вне ряда стандартных полотен — полотно задать при выборе модели; Д-4: раздвижная, полотно — по системе — полотно задать при выборе модели; Д-5: проём 730×2100 вне ряда стандартных полотен — полотно задать при выборе модели.


Схемы дверных блоков (1:25) — вид со стороны открывания; вершина треугольника — сторона петель

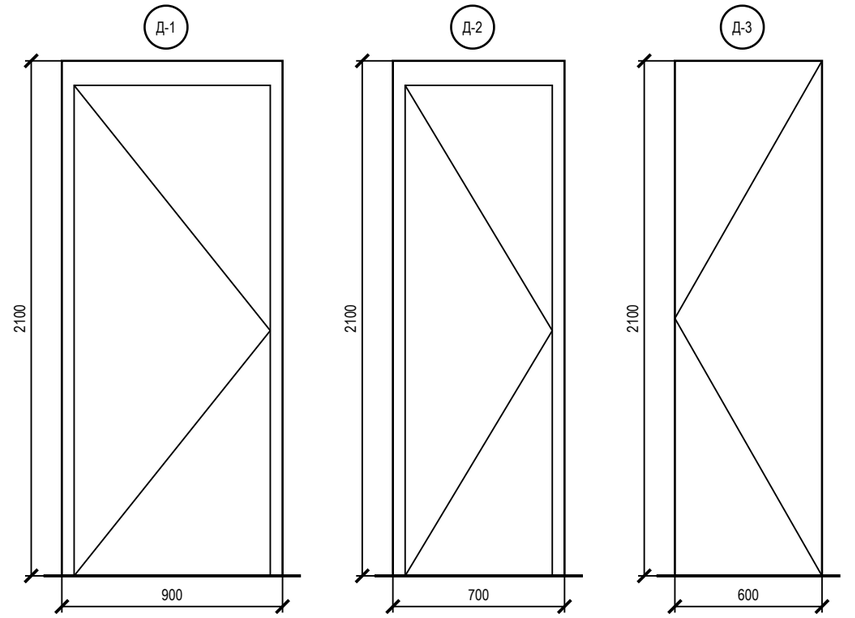

полотно 800×2000 (расч.)
откр. П, П, П, Л, П, П (схема — П, остальные по плану)

полотно 600×2000 (расч.)
откр. П, П, Л (схема — П, остальные по плану)

полотно не задано (записи реестра нет)
откр. Л

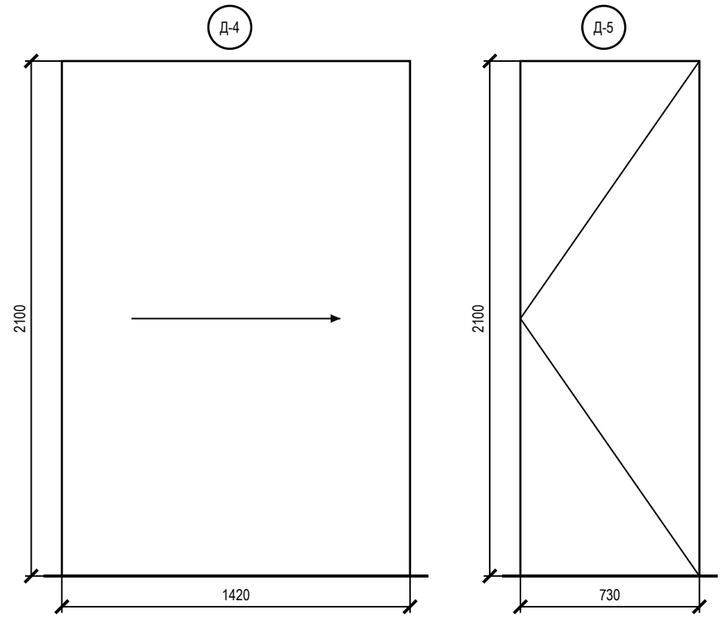


полотно не задано (записи реестра нет)
раздвижная

полотно не задано (записи реестра нет)
откр. Л

	Лист	№ док.	Подпись	Дата	Проект: Четырёхкомнатная квартира			
Дизайнер	Кырлан А.С.			14.11.26	Ведомость заполнения проёмов	Стадия	Лист	Листов
Проверил						П	50	147
Н. контр.								
Утв.								

выпуск 14.11.2026 № e7147312ff · стр. 50 из 147

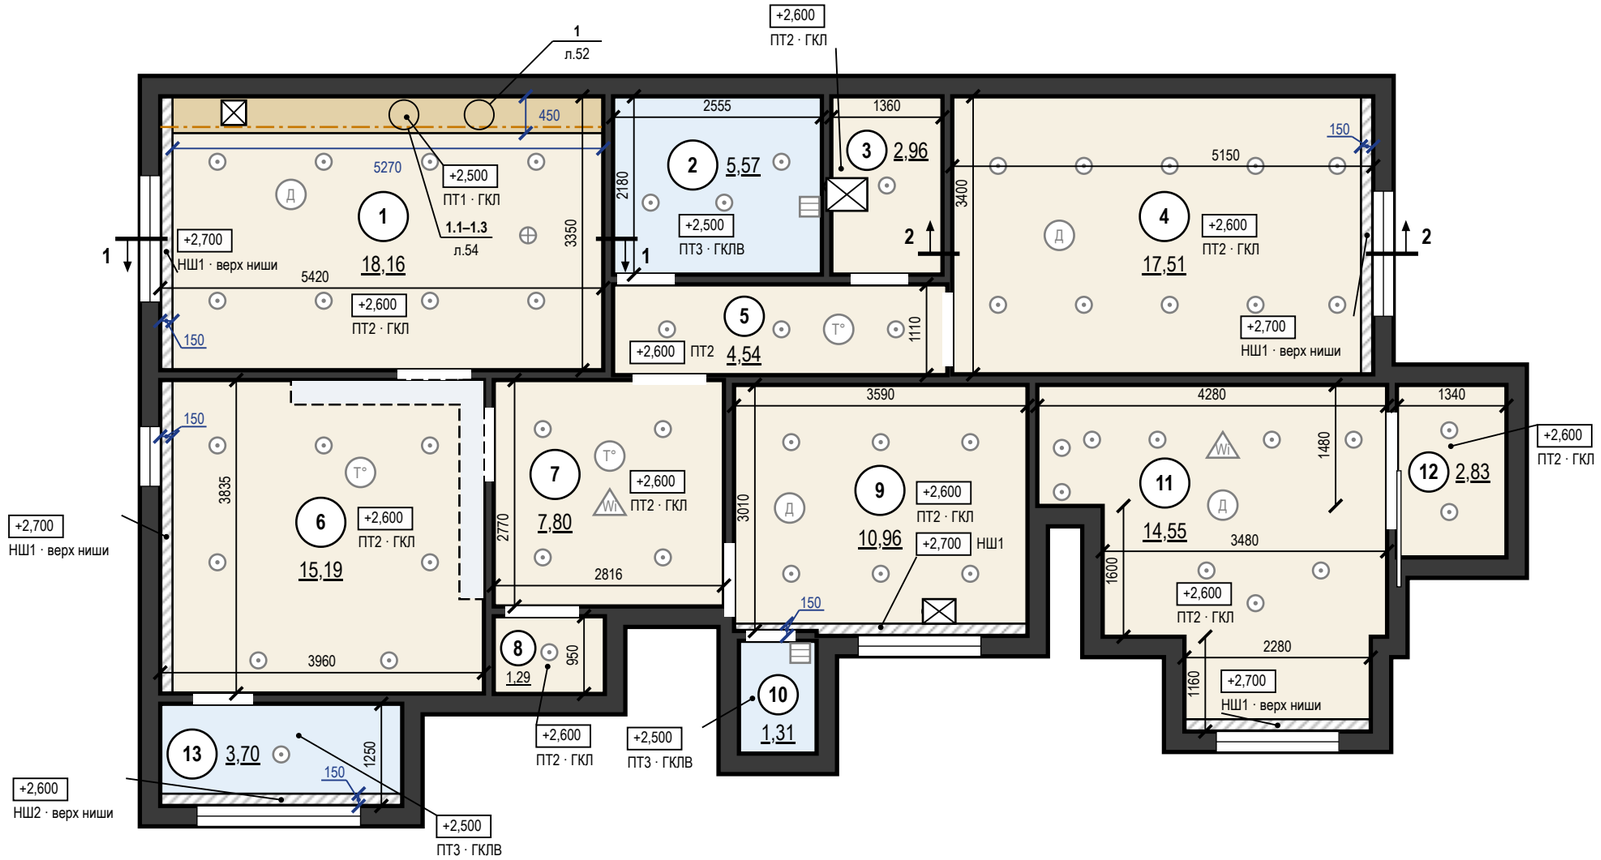

Ведомость потолков

Пом.	Марка	Конструкция	Низ / верх ниши	S, м²	Q
1	ПТ1	ГКЛ П113, короб LED	+2,500	2,37	Q3
1	ПТ2	ГКЛ П113	+2,600	15,29	Q3
1	НШ1	ниша под шторы 150×100	+2,700	0,50	
2	ПТ3	ГКЛВ П113	+2,500	5,57	Q3
3	ПТ2	ГКЛ П113	+2,600	2,96	Q3
4	ПТ2	То же	+2,600	17,00	Q3
4	НШ1	ниша под шторы 150×100	+2,700	0,51	
5	ПТ2	ГКЛ П113	+2,600	4,54	Q3
6	ПТ2	То же	+2,600	14,61	Q3
6	НШ1	ниша под шторы 150×100	+2,700	0,58	
7	ПТ2	ГКЛ П113	+2,600	7,80	Q3
8	ПТ2	То же	+2,600	1,29	Q3
9	ПТ2	То же	+2,600	10,48	Q3
9	НШ1	ниша под шторы 150×100	+2,700	0,48	
10	ПТ3	ГКЛВ П113	+2,500	1,31	Q3
11	ПТ2	ГКЛ П113	+2,600	14,21	Q3
11	НШ1	ниша под шторы 150×100	+2,700	0,34	
12	ПТ2	ГКЛ П113	+2,600	2,83	Q3
13	ПТ3	ГКЛВ П113	+2,500	3,26	Q3
13	НШ2	ниша под шторы 150×100	+2,600	0,44	
		Итого		**106,37**	

Примечания


1. За отметку ±0,000 принят уровень чистого пола сухих помещений (готовое покрытие), а не существующего пола; пол пом. 2, 10, 13 — −0,015, −0,030; верх плиты перекрытия −0,170 — расчётный по пирогу пола, не замерен; существующий пол снимается до плиты, его отметка не замерена. Отметки в прямоугольниках — низ потолка; низ плиты +2,700, +2,600. Марка потолка — одна конструкция и отметка на весь альбом.
2. Размеры помещений в свету (ширина × длина, мм), не поместившиеся на плане: пом. 3 — 1360 × 2180; пом. 5 — 4090 × 1110; пом. 8 — 1360 × 950; пом. 9 — 3590 × 3010, 2580 × 60; пом. 10 — 950 × 1380; пом. 12 — 1340 × 2110; пом. 13 — 2960 × 1250.
3. Потолки ГКЛ — каркасная система П113: подвесы через 1000 (с запасом: СП 163, табл. 14 — до 1100 при 0,15 кН/м²), несущие профили через 500, основные через 1200 мм; листы — поперёк несущих профилей. В помещениях 2, 10, 13 — ГКЛВ на оцинкованном каркасе.
4. LED-лента в алюминиевом профиле посередине карниза короба шириной 450 мм (узел 1, лист 52); длина по плану: пом. 1 — 5,4 м (в плане освещения 5,4).
5. Ниши под шторы 150×100 мм — на всю длину стены с окном; карниз — на закладной до обшивки (узел 2, лист 52).
6. Примыкание к стенам: теневой шов 15 мм, техзазор 3 мм — пом. 1, по стенам, выровненным штукатуркой (узел 1); пом. 2, 3, 4, 5, 6, 7, 8, 9, 10, 11, 12, 13 — разделительная лента.
7. Светильники и потолочные устройства — подложка с планов освещения, слаботочных систем и вентиляции (положение — по ним); вырезы и закладные — по ведомости на листе, до обшивки; отверстия не совмещать с профилями, глубина корпуса светильника до 70 мм.
8. Разрезы 1–1, 2–2 — на листе 52; высоты мебели и дверных блоков сверены с низом потолка в разрезах.
9. Шпаклевание ГКЛ и условия приёмки — Q3: рассеянный дневной свет, осмотр с 2 м; боковой свет не оценивается.
10. Ведомость вырезов и закладных в потолке — на листе 52; вырезы и закладные — до обшивки.
11. Пом. 6: короб воздуховода кухонной вытяжки ГКЛ 300×200 мм (ширина от стены × высота), низ +2,500, длина 4,44 м — по трассе плана вентиляции, вдоль стен до входа в канал под воздуховод Ø125; каркас ПН 28×27 по стене и плите, ПП 60×27, лист ГКЛ 12,5.
12. Люки ревизии 500×400, 400×300, 300×300 мм — по центру блоков питания LED (ревизия, ревизия, блок питания LED БП1; координаты — план освещения).
13. Сечения потолков М 1:10: пом. 4 — 4.1, 4.2 (лист 54); пом. 6 — 4.1, 4.2 (лист 54); пом. 9 — 4.1, 4.2 (лист 54); пом. 11 — 4.1, 4.2 (лист 54); пом. 13 — 13.1, 13.2 (листы 54, 55).

		Лист	№ док.	Подпись	Дата	Проект: Четырёхкомнатная квартира			М 1:75
Дизайнер	Кырлан А.С.				14.11.26	План потолков	Стадия	Лист	Листов
Проверил							П	51	147
Н. контр.									
Утв.									

выпуск 14.11.2026 № e7147312ff · стр. 51 из 147


Разрез 1–1 (М 1:40)

Пом. 1 Зал; линия разреза — план потолков, лист 51

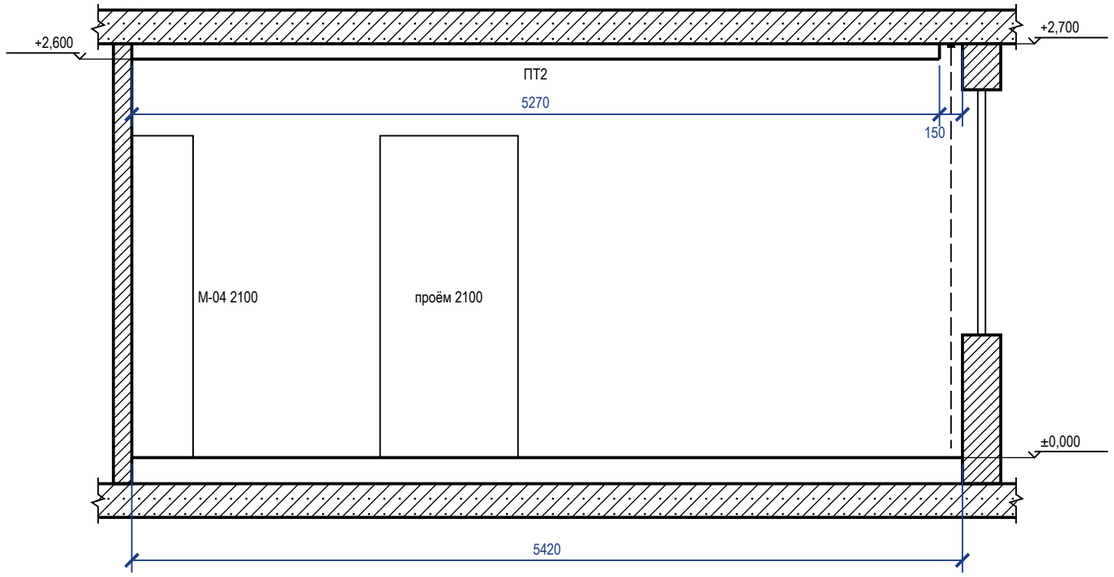


Разрез 2–2 (М 1:40)

Пом. 4 Детская 1; линия разреза — план потолков, лист 51

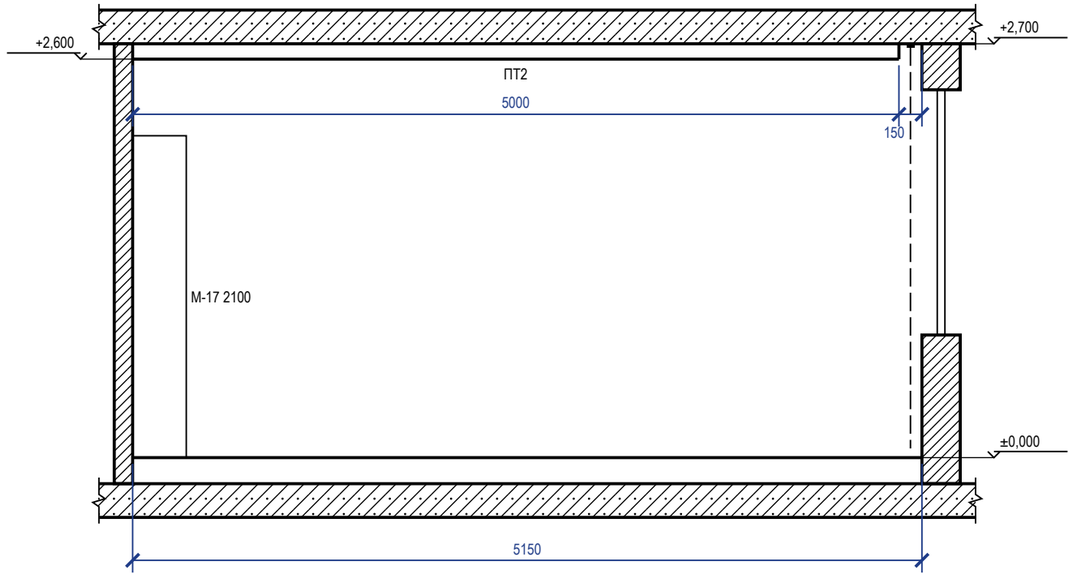

1 Короб с LED-подсветкой, теневой шов (М 1:10)


Пом. 1; карниз 150×100, щель под свет 60 мм

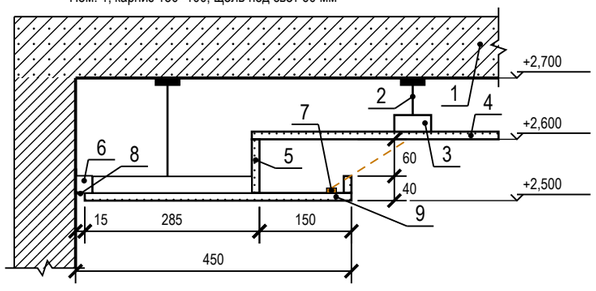

1 — плита перекрытия
2 — подвес прямой, шаг 1000 мм
3 — ПП 60×27: несущие через 500, основные через 1200 мм
4 — ГКЛ 12,5 по П113 — верхний уровень
5 — задняя стенка и бортик карниза — ГКЛ 12,5
6 — ПН 28×27 по периметру, к стене через 500 мм
7 — LED-лента в алюминиевом профиле
8 — теневой профиль: шов 15 мм, зазор 3 мм
9 — низ короба — ГКЛ 12,5 по ПП 60×27

2 Ниша под шторы (М 1:10)

Пом. 1, 4, 6, 9, 11, 13; без подсветки; закладные под карниз — до обшивки

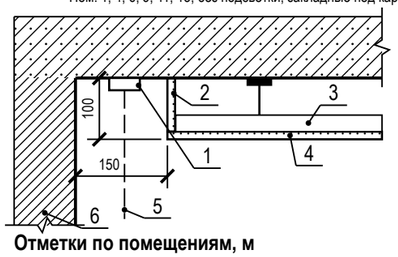

1 — карниз (шина), высота с верхом портьеры 80 мм
2 — стенка ниши — ГКЛ 12,5
3 — ПП 60×27 — каркас короба
4 — низ короба нижнего уровня — ГКЛ 12,5
5 — портьера
6 — стена с окном

Отметки по помещениям, м

Пом.	низ потолка	верх ниши	низ плиты
1, 4, 6, 9, 11	+2,600	+2,700	+2,700
13	+2,500	+2,600	+2,600

Ведомость вырезов и закладных в потолке

Марка	Устройство	Кол.	Пом.
	Светильник встраиваемый (марки — план освещения)	56	1, 2, 3, 4, 5, 6, 7, 8, 9, 10, 11, 12, 13
	Светильник подвесной (марки — план освещения)	1	1
ИП1, ИП2, ИП6, ИП7	Извещатель дымовой	4	1, 4, 9, 11
ИП3…ИП5	Извещатель тепловой	3	5, 6, 7
АР1, АР2	Точка доступа Wi-Fi, PoE	2	7, 11
ВР1, ВР3	Решётка вытяжная (вентилятор)	2	2, 10
	Люк ревизии 500×400, 400×300, 300×300	3	1, 3, 9

Условные обозначения

- плита перекрытия в сечении
- стена в сечении
- потолок ГКЛ в сечении; под линией — марка потолка (план потолков)
- мебель и дверные проёмы за секущей плоскостью; число — марка и верх от чистого пола, мм
- портьера в нише под шторы

Примечания

1. Разрезы — по линиям 1–1, 2–2 на плане потолков (лист 51). Отметки — от ±0,000 чистого пола, м; размеры — мм.
2. Высоты мебели и дверных блоков за секущей плоскостью сверены с низом потолка над ними: верх ниже низа короба и поля.
3. ГКЛ 12,5 мм по каркасу П113; перепад уровней и бортик карниза — ГКЛ по ПП 60×27 (узел 1 — на этом листе). Ниша под шторы — на всю длину стены с окном, карниз на закладной до обшивки (узел 2 — на этом листе).
4. Толщины плит перекрытия и пирога пола показаны условно.
5. Сечения потолков по помещениям М 1:10 (отметки помещения, профили, подвесы, крепёж, изделия) — листы 54–55.
6. Ведомость вырезов и закладных в потолке — к плану потолков (лист 51): вырезы и закладные — до обшивки, марки светильников — по плану освещения.
7. Ведомость объёмов потолков (лист ГКЛ, профиль, подвесы, лента, блоки питания, люки) — на листе 53.

	Лист	№ док.	Подпись	Дата
Дизайнер	Кырлан А.С.			14.11.26
Проверил				
Н. контр.				
Утв.				

Проект: Четырёхкомнатная квартира — **М 1:40; 1:10**

Разрезы и узлы потолков

Стадия	Лист	Листов
П	52	147

выпуск 14.11.2026 № e7147312ff · стр. 52 из 147

Ведомость объёмов потолков

Позиция	Ед.	Кол.	Пом.
Лист ГКЛ 12,5	м²	98,99	1, 3, 4, 5, 6, 7, 8, 9, 11, 12
Лист ГКЛВ 12,5	м²	10,88	2, 10, 13
Борта и карнизы (входят в площади листов выше)	м²	3,50	1, 4, 6, 9, 11, 13
Профиль ПП 60×27	м	307,26	1, 2, 3, 4, 5, 6, 7, 8, 9, 10, 11, 12, 13
Профиль ПН 28×27	м	198,10	1, 2, 3, 4, 5, 6, 7, 8, 9, 10, 11, 12, 13
Подвес прямой	шт.	102	1, 2, 3, 4, 5, 6, 7, 8, 9, 10, 11, 12, 13
Анкер-клин к плите	шт.	102	1, 2, 3, 4, 5, 6, 7, 8, 9, 10, 11, 12, 13
Шуруп TN 3,5×25	шт.	2527	1, 2, 3, 4, 5, 6, 7, 8, 9, 10, 11, 12, 13
Лента армирующая для швов	м	131,84	1, 2, 3, 4, 5, 6, 7, 8, 9, 10, 11, 12, 13
Шпаклёвка для швов	кг	43,95	1, 2, 3, 4, 5, 6, 7, 8, 9, 10, 11, 12, 13
Грунтовка (швы)	л	10,99	1, 2, 3, 4, 5, 6, 7, 8, 9, 10, 11, 12, 13
Лента разделительная по периметру	м	143,31	1, 2, 3, 4, 5, 6, 7, 8, 9, 10, 11, 12, 13
Сплошная шпаклёвка и окраска (площадь развёртки)	м²	109,87	1, 2, 3, 4, 5, 6, 7, 8, 9, 10, 11, 12, 13
Лента LED	м	5,42	1
Требуемая мощность блоков питания	Вт	68	1
Установленная мощность блоков питания	Вт	100	1
Блок питания LED	шт.	1	1
Люк ревизии	шт.	3	1, 3, 9

Примечания


1. ГКЛ 12,5 мм по каркасу П113; узлы коробов и ниш под шторы: узел 1 — лист 52; узел 2 — лист 52; условные обозначения разрезов — на листе 52.
2. Ведомость объёмов — по геометрии плана потолков: Лист ГКЛ 12,5 — плоскости уровней + борта (без арочных участков); Лист ГКЛВ 12,5 — плоскости уровней + борта; Борта и карнизы — длина перепада × перепад; Профиль ПП 60×27 — S × (1/шаг несущ. + 1/шаг осн.) + стойки бортов; Профиль ПН 28×27 — периметр стен + 2 × перепады + карнизы; Подвес прямой — по раскладке: S уровня / (шаг осн. × шаг подвесов), пояс уже шага — ряд вдоль пояса, фигура — по контуру; шаг подвесов — не больше табл. 14 СП 163; Анкер-клин к плите — по одному на подвес (Knauf П113); Шуруп TN 3,5×25 — 23 шт./м² (Knauf П113, табл. 2 альбома П 11); Лента армирующая для швов — 1,2 м/м² листа (Knauf); Шпаклёвка для швов — 0,4 кг/м² листа, только швы (Knauf); Грунтовка (швы) — 0,1 л/м² листа, только швы (Knauf); Лента разделительная по периметру — периметр стен под потолком ГКЛ; Сплошная шпаклёвка и окраска (площадь развёртки) — плоскости + борта; расход — по паспорту материала (норма расхода на сплошной слой не подтверждена); Лента LED — по оси карниза и ниши фигуры (план потолков); Требуемая мощность блоков питания — Вт/м × длина × 1,3; Установленная мощность блоков питания — сумма мощностей блоков по плану освещения; Блок питания LED — блоки потолочных лент по плану освещения (БП1); Люк ревизии — план потолков; без запаса на подрезку (при закупке листа: ×1,075 при S > 20 м², ×1,175 — 10–20 м², ×1,275 — < 10 м²).

	Лист	№ док.	Подпись	Дата	Проект: Четырёхкомнатная квартира			
Дизайнер	Кырлан А.С.			14.11.26				
Проверил					Разрезы и узлы потолков (продолжение)	Стадия	Лист	Листов
Н. контр.						П	53	147
Утв.								

выпуск 14.11.2026 № e7147312ff · стр. 53 из 147

Сечение 1.1. Короб с LED-подсветкой, теневой шов (М 1:10)


Пом. 1 Зал; карниз 150×100, щель под свет 60 мм

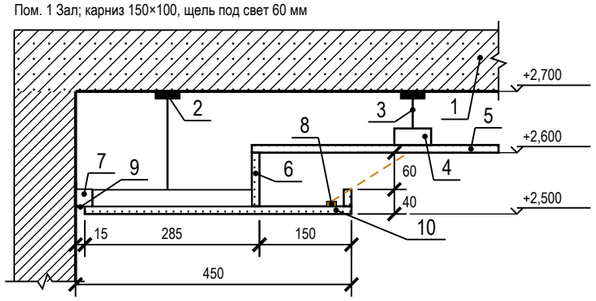

1 — плита перекрытия
2 — анкер-клин к плите — по одному на подвес
3 — подвес прямой, шаг 1000 мм
4 — ПП 60×27: несущие через 500, основные через 1200 мм; соединители одноуровневые, шурупы LN 3,5×9
5 — ГКЛ 12,5 по П113 — верхний уровень; шурупы TN 3,5×25 через 170 мм
6 — задняя стенка и бортик карниза — ГКЛ 12,5
7 — ПН 28×27 по периметру — дюбель-гвоздь через ≤ 500 мм, не менее 3 на профиль
8 — LED-лента 9,6 Вт/м, 24 В в алюминиевом профиле
9 — теневой профиль: шов 15 мм, зазор 3 мм
10 — низ короба — ГКЛ 12,5 по ПП 60×27

Сечение 1.2. Ниша под шторы (М 1:10)


Пом. 1 Зал; без подсветки; закладные под карниз — до обшивки

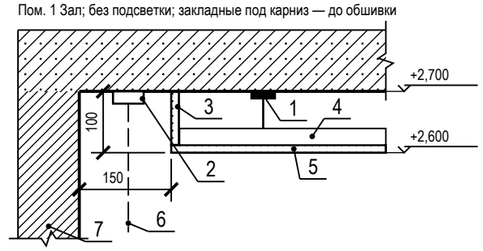

1 — анкер-клин к плите — по одному на подвес; подвес прямой, шаг 1000 мм
2 — карниз (шина), высота с верхом портьеры 80 мм
3 — стенка ниши — ГКЛ 12,5
4 — ПП 60×27 — каркас короба, основные через 1200 мм; соединители одноуровневые, шурупы LN 3,5×9
5 — низ короба нижнего уровня — ГКЛ 12,5; шурупы TN 3,5×25 через 170 мм
6 — портьера
7 — стена с окном

Сечение 1.3. Примыкание потолка к стене (М 1:10)


Пом. 1 Зал; примыкание — разделительная лента

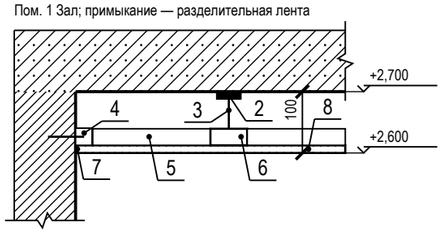

1 — плита перекрытия
2 — анкер-клин к плите — по одному на подвес
3 — подвес прямой, шаг 1000 мм
4 — ПН 28×27 по периметру — дюбель-гвоздь через ≤ 500 мм, не менее 3 на профиль
5 — ПП 60×27 несущий (вид) через 500 мм, в ПН
6 — ПП 60×27 основной (сечение) через 1200 мм; соединители одноуровневые, шурупы LN 3,5×9
7 — лента разделительная по стене, шов зашпаклёван
8 — ГКЛ 12,5 по П113; шурупы TN 3,5×25 через 170 мм

Сечение 4.1. Ниша под шторы (М 1:10)


Пом. 4 Детская 1, 6 Кухня, 9 Детская 2, 11 Гостиная; без подсветки; закладные под карниз — до обшивки

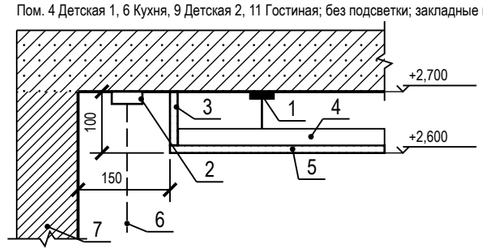

1 — анкер-клин к плите — по одному на подвес; подвес прямой, шаг 1000 мм
2 — карниз (шина), высота с верхом портьеры 80 мм
3 — стенка ниши — ГКЛ 12,5
4 — ПП 60×27 — каркас короба, основные через 1200 мм; соединители одноуровневые, шурупы LN 3,5×9
5 — низ короба нижнего уровня — ГКЛ 12,5; шурупы TN 3,5×25 через 170 мм
6 — портьера
7 — стена с окном

Сечение 4.2. Примыкание потолка к стене (М 1:10)


Пом. 4 Детская 1, 6 Кухня, 9 Детская 2, 11 Гостиная; примыкание — разделительная лента

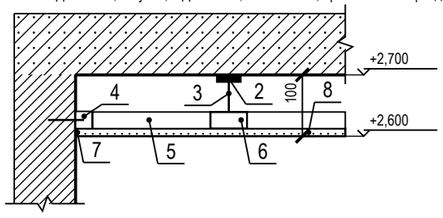

1 — плита перекрытия
2 — анкер-клин к плите — по одному на подвес
3 — подвес прямой, шаг 1000 мм
4 — ПН 28×27 по периметру — дюбель-гвоздь через ≤ 500 мм, не менее 3 на профиль
5 — ПП 60×27 несущий (вид) через 500 мм, в ПН
6 — ПП 60×27 основной (сечение) через 1200 мм; соединители одноуровневые, шурупы LN 3,5×9
7 — лента разделительная по стене, шов зашпаклёван
8 — ГКЛ 12,5 по П113; шурупы TN 3,5×25 через 170 мм

Сечение 13.1. Ниша под шторы (М 1:10)

Пом. 13 Балкон 1; без подсветки; закладные под карниз — до обшивки

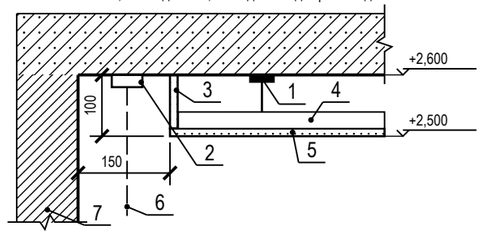

1 — анкер-клин к плите — по одному на подвес; подвес прямой, шаг 1000 мм
2 — карниз (шина), высота с верхом портьеры 80 мм
3 — стенка ниши — ГКЛВ 12,5
4 — ПП 60×27 — каркас короба, основные через 1200 мм; соединители одноуровневые, шурупы LN 3,5×9
5 — низ короба нижнего уровня — ГКЛВ 12,5; шурупы TN 3,5×25 через 170 мм
6 — портьера
7 — стена с окном

Условные обозначения

— - — LED-лента в нише подсветки (карниз короба, ниша фигуры)

Примечания


1. Сечения потолков М 1:10 по помещениям с нишами LED и нишами под шторы: отметки и размеры этого помещения от ±0,000 чистого пола (м, мм). Положение — по плану потолков (лист 51): короб и ниша LED — по линиям ленты, ниша под шторы — у стены с окном; типовые узлы по группам помещений — на листе 52.
2. Крепёж: подвес прямой к плите на анкер-клине — по одному на подвес (Knauf П113); ПН к стенам — дюбель-гвоздь через ≤ 500 мм, не менее 3 на профиль (серия 1.045.9-2.08); лист 12,5 — шурупы TN 3,5×25 через 170 мм (СП 163, табл. 15); профили между собой — соединители одноуровневые, шурупы LN 3,5×9.
3. Изделие карниза, профиля LED и галтели подписано артикулом из данных; где артикул не выбран, сечение дано по габаритам из данных (ширина и глубина ниши, щель под свет), изделие подбирается по ним.

	Лист	№ док.	Подпись	Дата	Проект: Четырёхкомнатная квартира			М 1:10
Дизайнер	Кырлан А.С.			14.11.26	Сечения потолков М 1:10	Стадия	Лист	Листов
Проверил						П	54	147
Н. контр.								
Утв.								

выпуск 14.11.2026 № e7147312ff · стр. 54 из 147

Сечение 13.2. Примыкание потолка к стене (М 1:10)

Пом. 13 Балкон 1; примыкание — разделительная лента

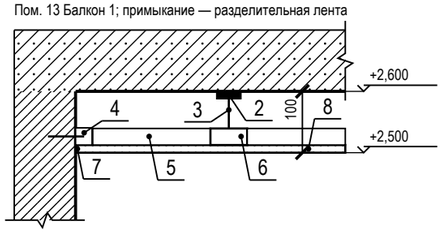

1 — плита перекрытия

2 — анкер-клин к плите — по одному на подвес

3 — подвес прямой, шаг 1000 мм

4 — ПН 28×27 по периметру — дюбель-гвоздь через ≤ 500 мм, не менее 3 на профиль

5 — ПП 60×27 несущий (вид) через 500 мм, в ПН

6 — ПП 60×27 основной (сечение) через 1200 мм; соединители одноуровневые, шурупы LN 3,5×9

7 — лента разделительная по стене, шов зашпаклёван

8 — ГКЛВ 12,5 по П113; шурупы TN 3,5×25 через 170 мм

Примечания

1. Сечения потолков М 1:10 по помещениям с нишами LED и нишами под шторы: отметки и размеры этого помещения от ±0,000 чистого пола (м, мм). Положение — по плану потолков (лист 51): короб и ниша LED — по линиям ленты, ниша под шторы — у стены с окном; типовые узлы по группам помещений — на листе 52.
2. Крепёж: подвес прямой к плите на анкер-клине — по одному на подвес (Knauf П113); ПН к стенам — дюбель-гвоздь через ≤ 500 мм, не менее 3 на профиль (серия 1.045.9-2.08); лист 12,5 — шурупы TN 3,5×25 через 170 мм (СП 163, табл. 15); профили между собой — соединители одноуровневые, шурупы LN 3,5×9.
3. Изделия карнизов, профилей LED и галтелей — по артикулу из данных.

	Лист	№ док.	Подпись	Дата	Проект: Четырёхкомнатная квартира			М 1:10
Дизайнер	Кырлан А.С.			14.11.26				
Проверил					Сечения потолков М 1:10	Стадия	Лист	Листов
Н. контр.						П	55	147
Утв.								

Условные обозначения

Данные щитка

Показатель	Значение
Номер щитка	ЩК
Тип	ЩРВ-П-72, IP41, навесной
Уст. мощность, кВт	29,75
Разреш. мощность, кВт	15
Расчётная, кВт	11,2
Автоматы 1п: занят. / рез.	19 / 4
Модулей: всего / занято	72 / 44
Ток на вводе, А	63
Вводной аппарат	QF0 C63, 1P+N
УЗИП	FV1, тип 2, ЩК, после счётчика
ГЗШ, проводник ОСУП	Cu 10 мм²
Листов схемы	2 (группы по листам)

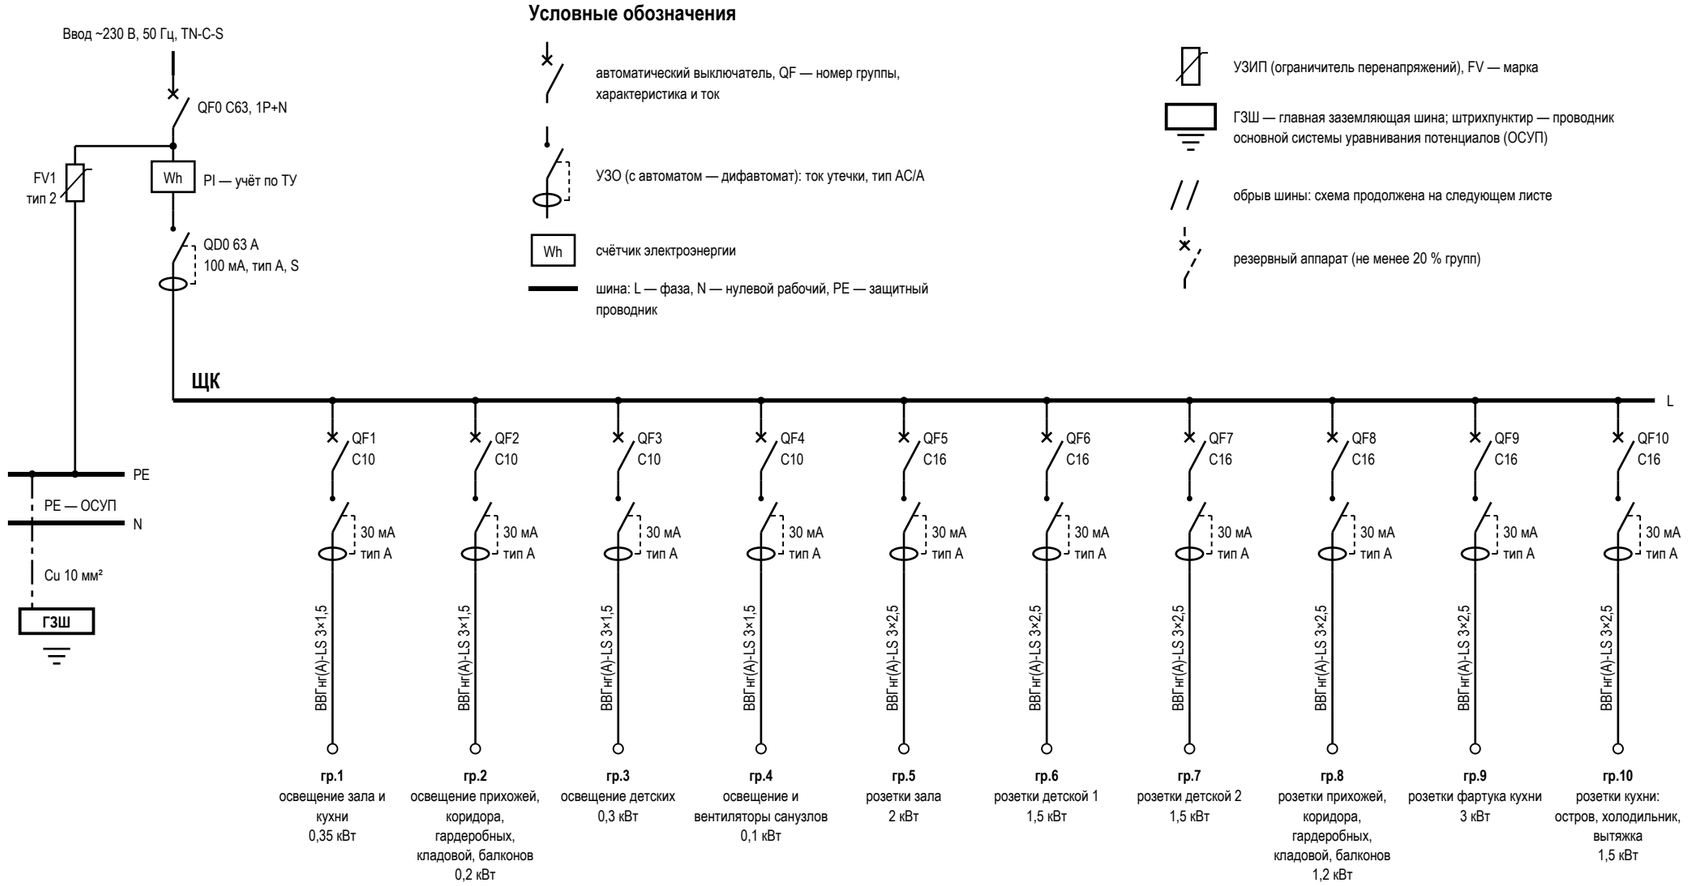


Таблица групп щита ЩК и кабельный журнал

№	Назначение	Помещения	Автомат	УЗО / дифавтомат	Кабель	Длина, м	Р, кВт	Точек
1	освещение зала и кухни	1, 6	C10	30 мА, тип A	ВВГнг(A)-LS 3×1,5	55,5	0,35	25
2	освещение прихожей, коридора, гардеробных, кладовой, балконов	3, 5, 7, 8, 12, 13	C10	30 мА, тип A	ВВГнг(A)-LS 3×1,5	111,7	0,2	19
3	освещение детских	4, 9, 11	C10	30 мА, тип A	ВВГнг(A)-LS 3×1,5	99,5	0,3	33
4	освещение и вентиляторы санузлов	2, 5, 10	C10	30 мА, тип A	ВВГнг(A)-LS 3×1,5	34,7	0,1	9
5	розетки зала	1	C16	30 мА, тип A	ВВГнг(A)-LS 3×2,5	27,6	2	6
6	розетки детской 1	4	C16	30 мА, тип A	ВВГнг(A)-LS 3×2,5	32,8	1,5	5
7	розетки детской 2	9	C16	30 мА, тип A	ВВГнг(A)-LS 3×2,5	24,1	1,5	4
8	розетки прихожей, коридора, гардеробных, кладовой, балконов	3, 5, 7, 12, 13	C16	30 мА, тип A	ВВГнг(A)-LS 3×2,5	72,9	1,2	6
9	розетки фартука кухни	6	C16	30 мА, тип A	ВВГнг(A)-LS 3×2,5	18,3	3	4
10	розетки кухни: остров, холодильник, вытяжка	6	C16	30 мА, тип A	ВВГнг(A)-LS 3×2,5	19,6	1,5	6

Примечания

1. Схема однолинейная: одна линия — фаза, N и PE группы; аппараты — в отключённом положении (ГОСТ 2.702, ГОСТ 2.755). Номера групп — как у точек на планах (гр.). За отметку 0,000 принят уровень чистого пола; высота щита — по плану розеток.
2. Розеточные и мокрые линии — через УЗО или дифавтомат с током утечки не более 30 мА (ПУЭ 7.1.79); в санузле выполнить ДСУП (ПУЭ 7.1.87–7.1.88).
3. УЗО тип A — для линий с электроникой, стиральной и посудомоечной машиной, LED-драйверами; тип AC — только для чисто активной нагрузки.
4. Кабель — медный, исполнение нг(A)-LS (ГОСТ 31565-2012); скрытая прокладка только горизонтально и вертикально, фактические трассы зафиксировать исполнительной схемой до закрытия отделкой.
5. Номинал автомата — не выше допустимого тока кабеля: 1,5 мм² — до 10 А, 2,5 мм² — до 16 А. Резерв щита — не менее 20 % модулей.
6. Расчёт нагрузок, токов КЗ, селективности и сечений — по проекту ЭОМ организации с допуском СРО; лист задаёт состав, расположение и группы.
7. УЗИП FV1 — после вводного автомата, проводник к шине PE — кратчайший, без петель. Шина PE щита соединяется с ГЗШ проводником ОСУП; к ГЗШ присоединяются трубы водопровода и отопления на вводе в квартиру (ПУЭ 7.1.87). Шины N и PE — раздельные, после разделения PEN не объединяются.
8. До подключения нагрузки — приёмо-сдаточные испытания с протоколом: сопротивление изоляции линий не менее 0,5 МОм, срабатывание УЗО по току и времени, непрерывность защитных проводников PE (ПУЭ, гл. 1.8).

	Лист	№ док.	Подпись	Дата	Проект: Четырёхкомнатная квартира			
Дизайнер	Кырлан А.С.			14.11.26	Однолинейная схема щита	Стадия	Лист	Листов
Проверил						П	56	147
Н. контр.								
Утв.								

Продолжение однолинейной схемы щита ЩК, начало — лист 56

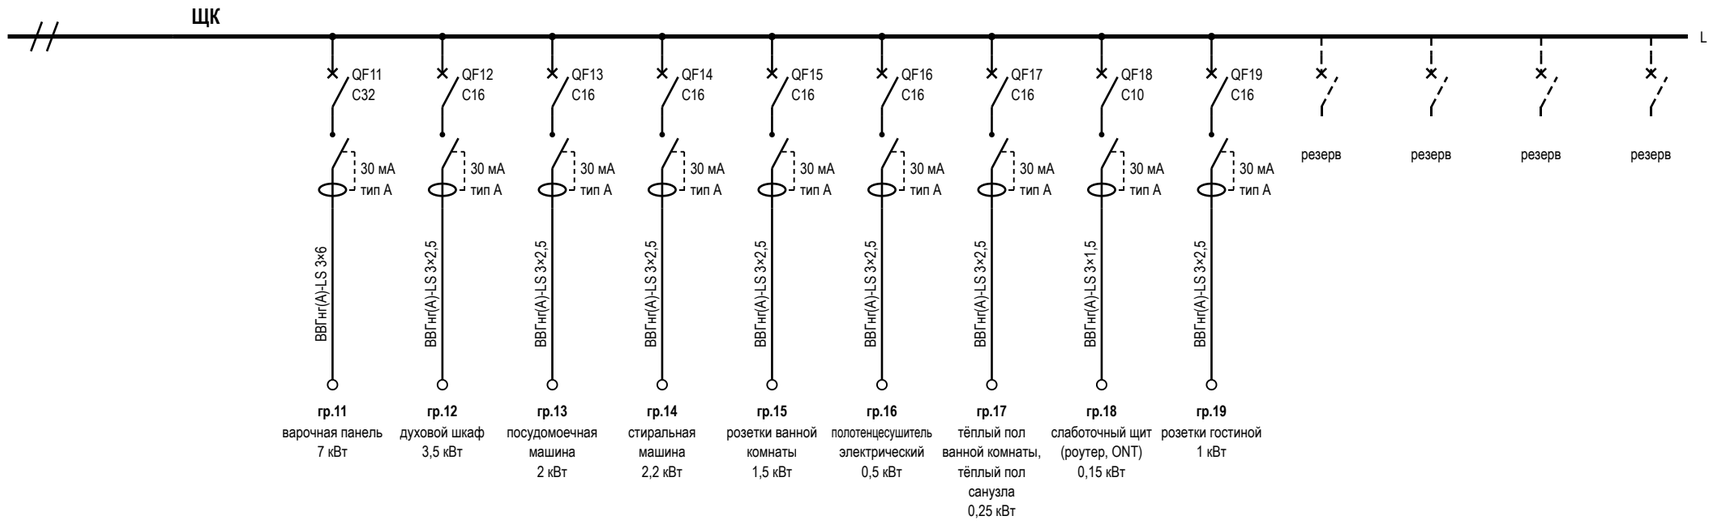


Таблица групп щита ЩК и кабельный журнал (продолжение)

№	Назначение	Помещения	Автомат	УЗО / дифавтомат	Кабель	Длина, м	Р, кВт	Точек
11	варочная панель	6	C32	30 мА, тип А	ВВГнг(А)-LS 3×6	9,8	7	1
12	духовой шкаф	6	C16	30 мА, тип А	ВВГнг(А)-LS 3×2,5	8,9	3,5	1
13	посудомоечная машина	6	C16	30 мА, тип А	ВВГнг(А)-LS 3×2,5	7,3	2	1
14	стиральная машина	2	C16	30 мА, тип А	ВВГнг(А)-LS 3×2,5	13,8	2,2	1
15	розетки ванной комнаты	2	C16	30 мА, тип А	ВВГнг(А)-LS 3×2,5	13,2	1,5	1
16	полотенцесушитель электрический	2	C16	30 мА, тип А	ВВГнг(А)-LS 3×2,5	15,7	0,5	1
17	тёплый пол ванной комнаты, тёплый пол санузла	2, 10	C16	30 мА, тип А	ВВГнг(А)-LS 3×2,5	24	0,25	2
18	слаботочный щит (роутер, ONT)	7	C10	30 мА, тип А	ВВГнг(А)-LS 3×1,5	6	0,15	1
19	розетки гостиной	11	C16	30 мА, тип А	ВВГнг(А)-LS 3×2,5	25,7	1	3
	Итого по сечениям ВВГнг(А)-LS (все группы щита), м: 3×1,5 — 307,4; 3×2,5 — 303,9; 3×6 — 9,8					621,1		

Примечания

1. Лист — продолжение однолинейной схемы щита ЩК: начало, данные щитка и условные обозначения — лист 56. Ввод, учёт, вводной аппарат, УЗИП, шины N и PE и ГЗШ показаны там же; шина L листа — та же шина щита.
2. Схема однолинейная: одна линия — фаза, N и PE группы; аппараты — в отключённом положении (ГОСТ 2.702, ГОСТ 2.755). Номера групп — как у точек на планах (гр.). За отметку 0,000 принят уровень чистого пола; высота щита — по плану розеток.
3. Розеточные и мокрые линии — через УЗО или дифавтомат с током утечки не более 30 мА (ПУЭ 7.1.79); в санузле выполнить ДСУП (ПУЭ 7.1.87–7.1.88).
4. УЗО тип А — для линий с электроникой, стиральной и посудомоечной машиной, LED-драйверами; тип АС — только для чисто активной нагрузки.
5. Кабель — медный, исполнение нг(А)-LS (ГОСТ 31565-2012); скрытая прокладка только горизонтально и вертикально, фактические трассы зафиксировать исполнительной схемой до закрытия отделкой.
6. Номинал автомата — не выше допустимого тока кабеля: 1,5 мм² — до 10 А, 2,5 мм² — до 16 А. Резерв щита — не менее 20 % модулей.
7. Расчёт нагрузок, токов КЗ, селективности и сечений — по проекту ЭОМ организации с допуском СРО; лист задаёт состав, расположение и группы.
8. До подключения нагрузки — приёмо-сдаточные испытания с протоколом: сопротивление изоляции линий не менее 0,5 МОм, срабатывание УЗО по току и времени, непрерывность защитных проводников PE (ПУЭ, гл. 1.8).

	Лист	№ док.	Подпись	Дата	Проект: Четырёхкомнатная квартира			
Дизайнер	Кырлан А.С.			14.11.26				
Проверил					Однолинейная схема щита (продолжение)	Стадия	Лист	Листов
Н. контр.								
Утв.						П	57	147

Группы щита ЩК (1)

№	Назначение	Руст, кВт	Кс	Ррасч, кВт	Iрасч, А	Автомат	Кабель
1	освещение зала и кухни	0,35	0,6	0,21	1	C10	3×1,5
2	освещение прихожей, коридора, гардеробных, кладовой, балконов	0,2	0,6	0,12	0,5	C10	3×1,5
3	освещение детских	0,3	0,6	0,18	0,8	C10	3×1,5
4	освещение и вентиляторы санузлов	0,1	0,6	0,06	0,3	C10	3×1,5
5	розетки зала	2	0,4	0,8	3,7	C16	3×2,5
6	розетки детской 1	1,5	0,4	0,6	2,7	C16	3×2,5
7	розетки детской 2	1,5	0,4	0,6	2,7	C16	3×2,5
8	розетки прихожей, коридора, гардеробных, кладовой, балконов	1,2	0,4	0,48	2,2	C16	3×2,5
9	розетки фартука кухни	3	0,4	1,2	5,5	C16	3×2,5
10	розетки кухни: остров, холодильник, вытяжка	1,5	0,4	0,6	2,7	C16	3×2,5

Группы щита ЩК (2)

№	Назначение	Руст, кВт	Кс	Ррасч, кВт	Iрасч, А	Автомат	Кабель
11	варочная панель	7	0,6	4,2	19,2	C32	3×6
12	духовой шкаф	3,5	0,6	2,1	9,6	C16	3×2,5
13	посудомоечная машина	2	0,7	1,4	6,4	C16	3×2,5
14	стиральная машина	2,2	0,7	1,54	7	C16	3×2,5
15	розетки ванной комнаты	1,5	0,7	1,05	4,8	C16	3×2,5
16	полотенцесушитель электрический	0,5	0,7	0,35	1,6	C16	3×2,5
17	тёплый пол ванной комнаты, тёплый пол санузла	0,25	1	0,25	1,1	C16	3×2,5
18	слаботочный щит (роутер, ONT)	0,15	0,4	0,06	0,3	C10	3×1,5
19	розетки гостиной	1	0,4	0,4	1,8	C16	3×2,5

Итог по квартире

Показатель	Значение
Установленная мощность Σ Руст	29,75 кВт
Σ Руст × Кс по группам	16,2 кВт
Коэффициент одновременности	0,7
Расчётная мощность квартиры Ррасч	11,3 кВт
Расчётный ток Iрасч (230 В, cosφ 0,95)	52 А
Разрешённая мощность	15 кВт
Запас до разрешённой	24,4 %
Вводной аппарат	C63, 1P+N


Примечания

1. Руст — установленная мощность группы по данным щита (приборы — по паспорту, розетки общего назначения — оценка 0,1 кВт на гнездо). Кс — коэффициенты спроса: освещение 0,6; розетки 0,4; варочная и духовой 0,6; кондиционеры 0,8; тёплый пол 1,0; прочие 0,7; одновременность 0,7.
2. Коэффициенты — ориентир исполнителя, не табличные значения нормы; расчёт нагрузки подтверждает инженер ЭОМ (СП 256.1325800.2016). Под разрешённую мощность они не подгоняются.
3. Вывод: запас 24 % (расчётная 11,3 кВт при разрешённой 15 кВт).
4. Розеточные и мокрые линии — через УЗО или дифавтомат с током утечки не более 30 мА (ПУЭ 7.1.79); в санузле выполнить ДСУП (ПУЭ 7.1.87–7.1.88).

	Лист	№ док.	Подпись	Дата	Проект: Четырёхкомнатная квартира			
Дизайнер	Кырлан А.С.			14.11.26	Таблица нагрузок щита	Стадия	Лист	Листов
Проверил						П	58	147
Н. контр.								
Утв.								

выпуск 14.11.2026 № e7147312ff · стр. 58 из 147

План принципиальных трасс (М 1:100)

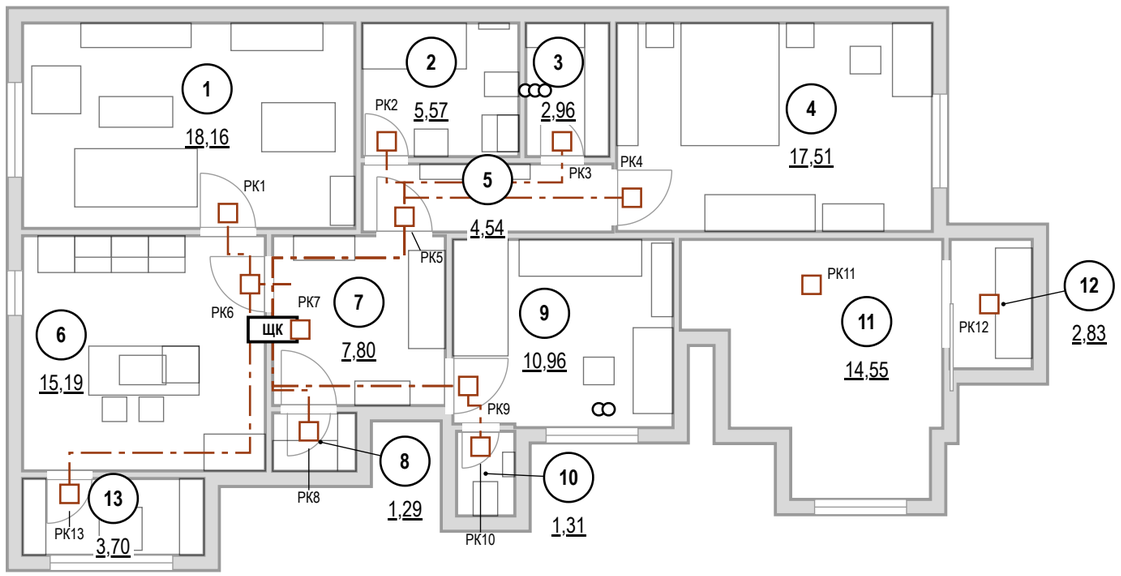

Кабель по группам ВВГнг(А)-LS, м

Гр.	мм²	Трасса	Данные
1	3×1,5	55,5	55,5
2	3×1,5	98,7	111,7
3	3×1,5	99,1	99,5
4	3×1,5	33,3	34,7
5	3×2,5	27,6	27,6
6	3×2,5	30,3	32,8
7	3×2,5	24,1	24,1
8	3×2,5	72,7	72,9
9	3×2,5	18,6	18,3
10	3×2,5	19,6	19,6

Гр.	мм²	Трасса	Данные
11	3×6	9,8	9,8
12	3×2,5	8,9	8,9
13	3×2,5	7,3	7,3
14	3×2,5	13,4	13,8
15	3×2,5	12,7	13,2
16	3×2,5	15,3	15,7
17	3×2,5	23,3	24
18	3×1,5	6	6
19	3×2,5	25,7	25,7
Σ		**601,9**	**621,1**

Экспликация помещений

№	Помещение	Площадь, м²
1	Зал	18,16
2	Ванная комната	5,57
3	Тёмная комната	2,96
4	Детская 1	17,51
5	Коридор	4,54
6	Кухня	15,19
7	Прихожая-коридор	7,80
8	Гардеробная 2	1,29
9	Детская 2	10,96
10	Санузел	1,31
11	Гостиная	14,55
12	Гардеробная 1	2,83
13	Балкон 1 *	3,70
	Итого (общая площадь)	102,67

Объёмы прокладки

Работа, материал	Ед.	Кол.
Гофротруба Ø20 в потолочном пространстве	м	280,1
Кабель-канал плинтуса для силовых линий	м	127,9
Короб или накладной канал для вертикальных спусков и подъёмов	м	98,9
Коробка распределительная (РК) над дверью помещения	шт	13
Слаботочка: Кабель коаксиальный RG-6 (75 Ом) к розеткам ТВ	м	14,5
Слаботочка: U/UTP кат. 6 (LAN, Wi-Fi, камеры)	м	72,7
Слаботочка: гофротруба Ø20 отдельно от силовых	м	78,5

Штробы — только после заключения

Работа	Ед.	Кол.
Вертикальные штробы 20×20 мм от потолка до каждой настенной точки (в маршрут без штроб не входят)	м	109,9

Условные обозначения


- ЩК — щит квартирный
- РК — распределительная коробка над дверью помещения
- магистраль от щита к РК: потолочное пространство, гофра
- мебель и сантехприборы — подложка

Примечания

1. За отметку 0,000 принят уровень чистого пола. Высоты Н — от чистого пола до оси изделия; привязки — от чистовой грани стены до оси механизма (у рамки на несколько постов — до оси рамки).
2. Розеточные и мокрые линии — через УЗО или дифавтомат с током утечки не более 30 мА (ПУЭ 7.1.79); в санузле выполнить ДСУП (ПУЭ 7.1.87–7.1.88).
3. Кабель — медный, исполнение нг(А)-LS (ГОСТ 31565-2012); скрытая прокладка только горизонтально и вертикально, фактические трассы зафиксировать исполнительной схемой до закрытия отделкой.
4. Расчёт нагрузок, токов КЗ, селективности и сечений — по проекту ЭОМ организации с допуском СРО; лист задаёт состав, расположение и группы.
5. Длины — по плану: от щита вверх в потолочное пространство, по дверям и коридору без захода в мокрые помещения к распределительной коробке над дверью, далее к точкам; вертикали считаются вниз и обратно (у последней точки цепочки — в один конец); запас 10 %. Трассы принципиальные: фактическую зафиксировать исполнительной схемой до закрытия отделкой.
6. Несущие стены не определены: штробы в стенах не выполнять. Маршрут проложен без штроб: горизонтали — за потолком в гофре (280,1 м) и в кабель-канале плинтуса (127,9 м), вертикали — в коробе или накладном канале (174 м кабеля). Точек: за потолком — 60, спуск из потолка — 11, по плинтусу — 23, плинтус и подъём — 35.
7. Вариант со штробами — работа после технического заключения: 109,9 м вертикальных штроб от потолка до каждой настенной точки; условие — только после технического заключения: стена не несущая (или вертикальная штроба в несущей согласована конструктором), глубина и ширина 20–25 мм, не в зонах 0–2 ванной. Без заключения и согласования конструктора в смету и в график эта работа не входит.
8. В данных проекта (журнал щита) длины кабеля внесены оценкой (621 м), по трассам из геометрии — 602 м (-3 %): к закупке и в смету принимать длины по трассам, а оценку в данных проекта заменить.
9. Слаботочные сети: кабели и точки считаются по лучам от ЩС (лист слаботочных сетей): 87 м, портов патч-панели и коммутатора не менее 6; из точек 3 предложения листа слаботочки, не подтверждённые заказчиком. Изделия — в ведомости изделий.

	Лист	№ док.	Подпись	Дата	Проект: Четырёхкомнатная квартира			М 1:100
Дизайнер	Кырлан А.С.			14.11.26	План принципиальных трасс	Стадия	Лист	Листов
Проверил						П	59	147
Н. контр.								
Утв.								

План розеток (М 1:75)

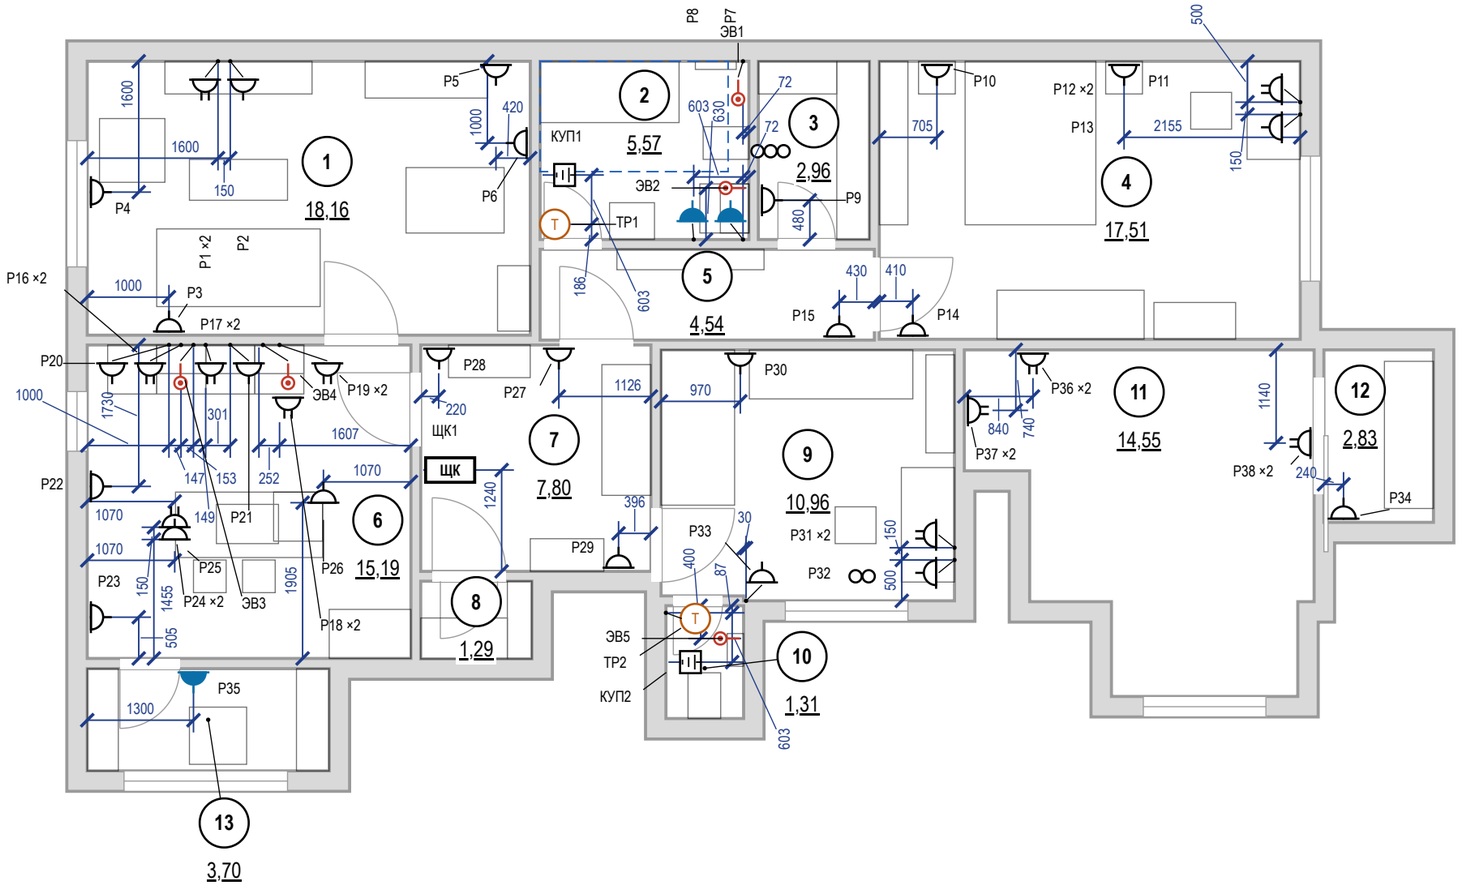

Условные обозначения

Знак	Тип изделия	Н, мм	Кол., шт
	Розетка с заземлением	300	13
	То же	у знака	11
	Блок розеток с заземлением, рамка 2 поста	300	3
	То же	у знака	8
	Розетка с заземлением IP44	300	1
	То же	у знака	2
	Вывод кабеля к прибору	у знака	5
КУП	КУП (уравнивание потенциалов)	353	2
Т	Терморегулятор тёплого пола	956	2
ЩК	Щит квартирный	1600	1

- розетка с заземляющим контактом; у знака — марка и ×N — число постов в рамке; группа щита, высота оси и назначение — в ведомости точек
- знак разведён для читаемости: точка на стене — у выноски, привязка — до неё
- граница зоны 2 ванной (600 мм от ванны/поддона)
- мебель и сантехприборы — подложка
- стояк: К1 — канализация, В1 — ХВС, Т3 — ГВС
- 1 — номер помещения, площадь м²

Итого розеток (механизмов) — 49 шт; рамок — 38 шт: на 1 пост — 27, на 2 поста — 11.


Примечания

1. За отметку 0,000 принят уровень чистого пола. Высоты Н — от чистого пола до оси изделия; привязки — от чистовой грани стены до оси механизма (у рамки на несколько постов — до оси рамки).
2. Высоты Н и группы щита — в ведомости электроточек: розетки — 300 мм от чистого пола до оси механизма, если в ведомости не указано иное; выводы кабеля — по паспорту прибора.
3. Розетки в санузле — только вне зон 0–2 (ПУЭ 7.1.48, ГОСТ Р 50571.7.701-2024), IP44, через УЗО 30 мА.
4. Розеточные и мокрые линии — через УЗО или дифавтомат с током утечки не более 30 мА (ПУЭ 7.1.79); в санузле выполнить ДСУП (ПУЭ 7.1.87–7.1.88).
5. Кабель — медный, исполнение нг(А)-LS (ГОСТ 31565-2012); скрытая прокладка только горизонтально и вертикально, фактические трассы зафиксировать исполнительной схемой до закрытия отделкой.
6. Расчёт нагрузок, токов КЗ, селективности и сечений — по проекту ЭОМ организации с допуском СРО; лист задаёт состав, расположение и группы.

	Лист	№ док.	Подпись	Дата	Проект: Четырёхкомнатная квартира			М 1:75
Дизайнер	Кырлан А.С.			14.11.26	План розеток и электровыводов	Стадия	Лист	Листов
Проверил						П	60	147
Н. контр.								
Утв.								

выпуск 14.11.2026 № e7147312ff · стр. 60 из 147

План слаботочных сетей (М 1:50)

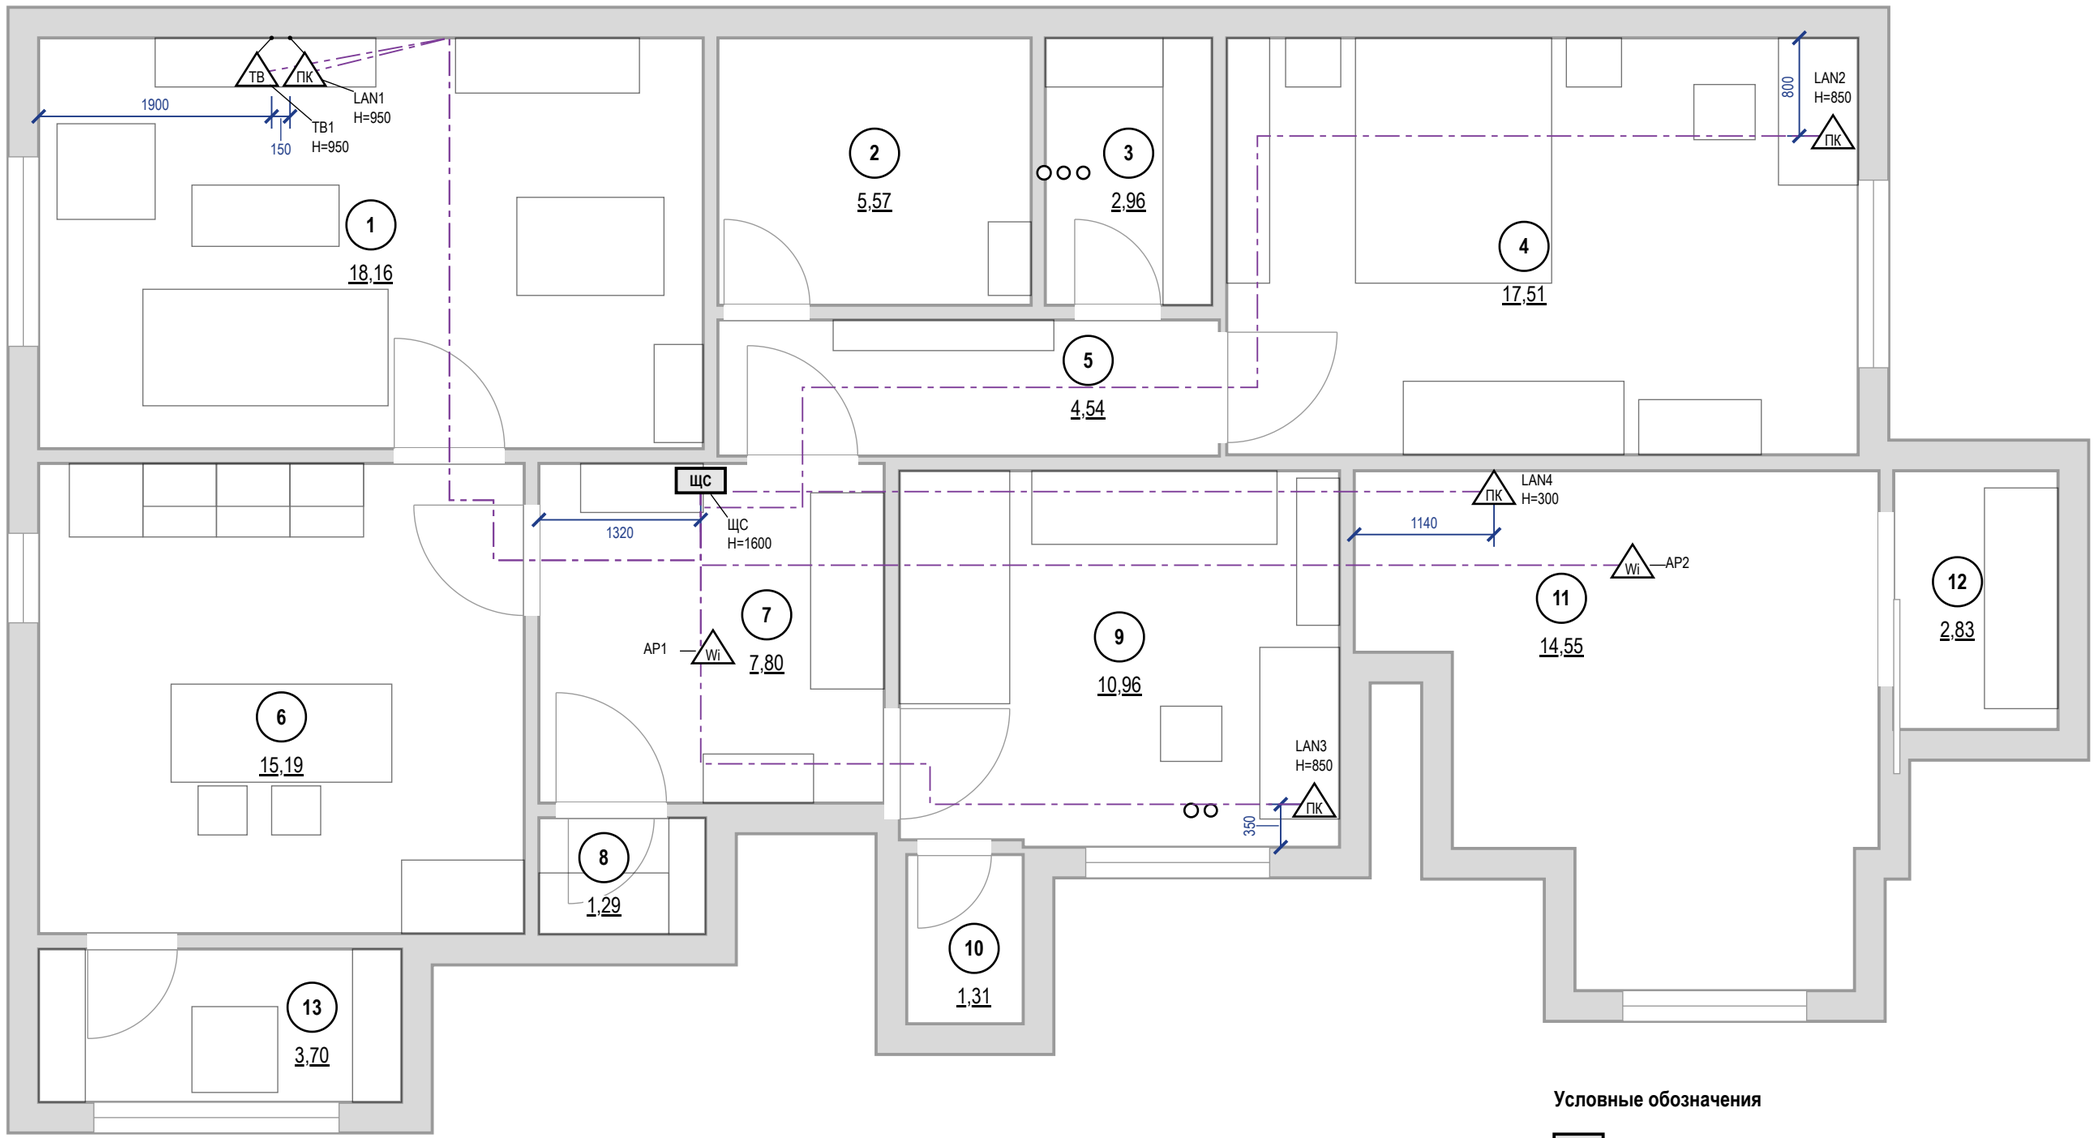

Условные обозначения

ЩС	щит слаботочный: ввод провайдера, роутер, коммутатор
ПК	розетка компьютерная RJ45
ТВ	розетка телевизионная
Wi	точка доступа Wi-Fi (питание PoE)
— — —	кабель от ЩС до точки, отдельным лучом
▭	мебель и сантехприборы — подложка
○	стояк: К1 — канализация, В1 — ХВС, Т3 — ГВС
1	номер помещения, площадь м²


Примечания

1. За отметку 0,000 принят уровень чистого пола. Высоты Н — от чистого пола до оси изделия; привязки — от чистовой грани стены до оси механизма (у рамки на несколько постов — до оси рамки).
2. Высота установки, не указанная на плане: розетки LAN и ТВ — 300 мм от чистого пола.
3. Слаботочные кабели — отдельно от силовых: в своей трубе или лотке, при параллельной прокладке не ближе 100 мм к силовым, пересечения под прямым углом; каждую точку — отдельным кабелем от ЩС без скруток.
4. Трассы на листе — принципиальные; фактические зафиксировать исполнительной схемой до закрытия отделкой. Силовые линии, УЗО 30 мА, ДСУП, кабель нг(А)-LS — по листам розеток и щита.
5. Проект силовой части и расчёт токов КЗ — по проекту ЭОМ; слаботочная часть согласуется с провайдером и управляющей компанией (домофон, коллективное ТВ).

	Лист	№ док.	Подпись	Дата	Проект: Четырёхкомнатная квартира	М 1:50		
Дизайнер	Кырлан А.С.			14.11.26	План слаботочных сетей	Стадия	Лист	Листов
Проверил						П	61	147
Н. контр.								
Утв.								

выпуск 14.11.2026 № e7147312ff · стр. 61 из 147

План освещения (М 1:50)

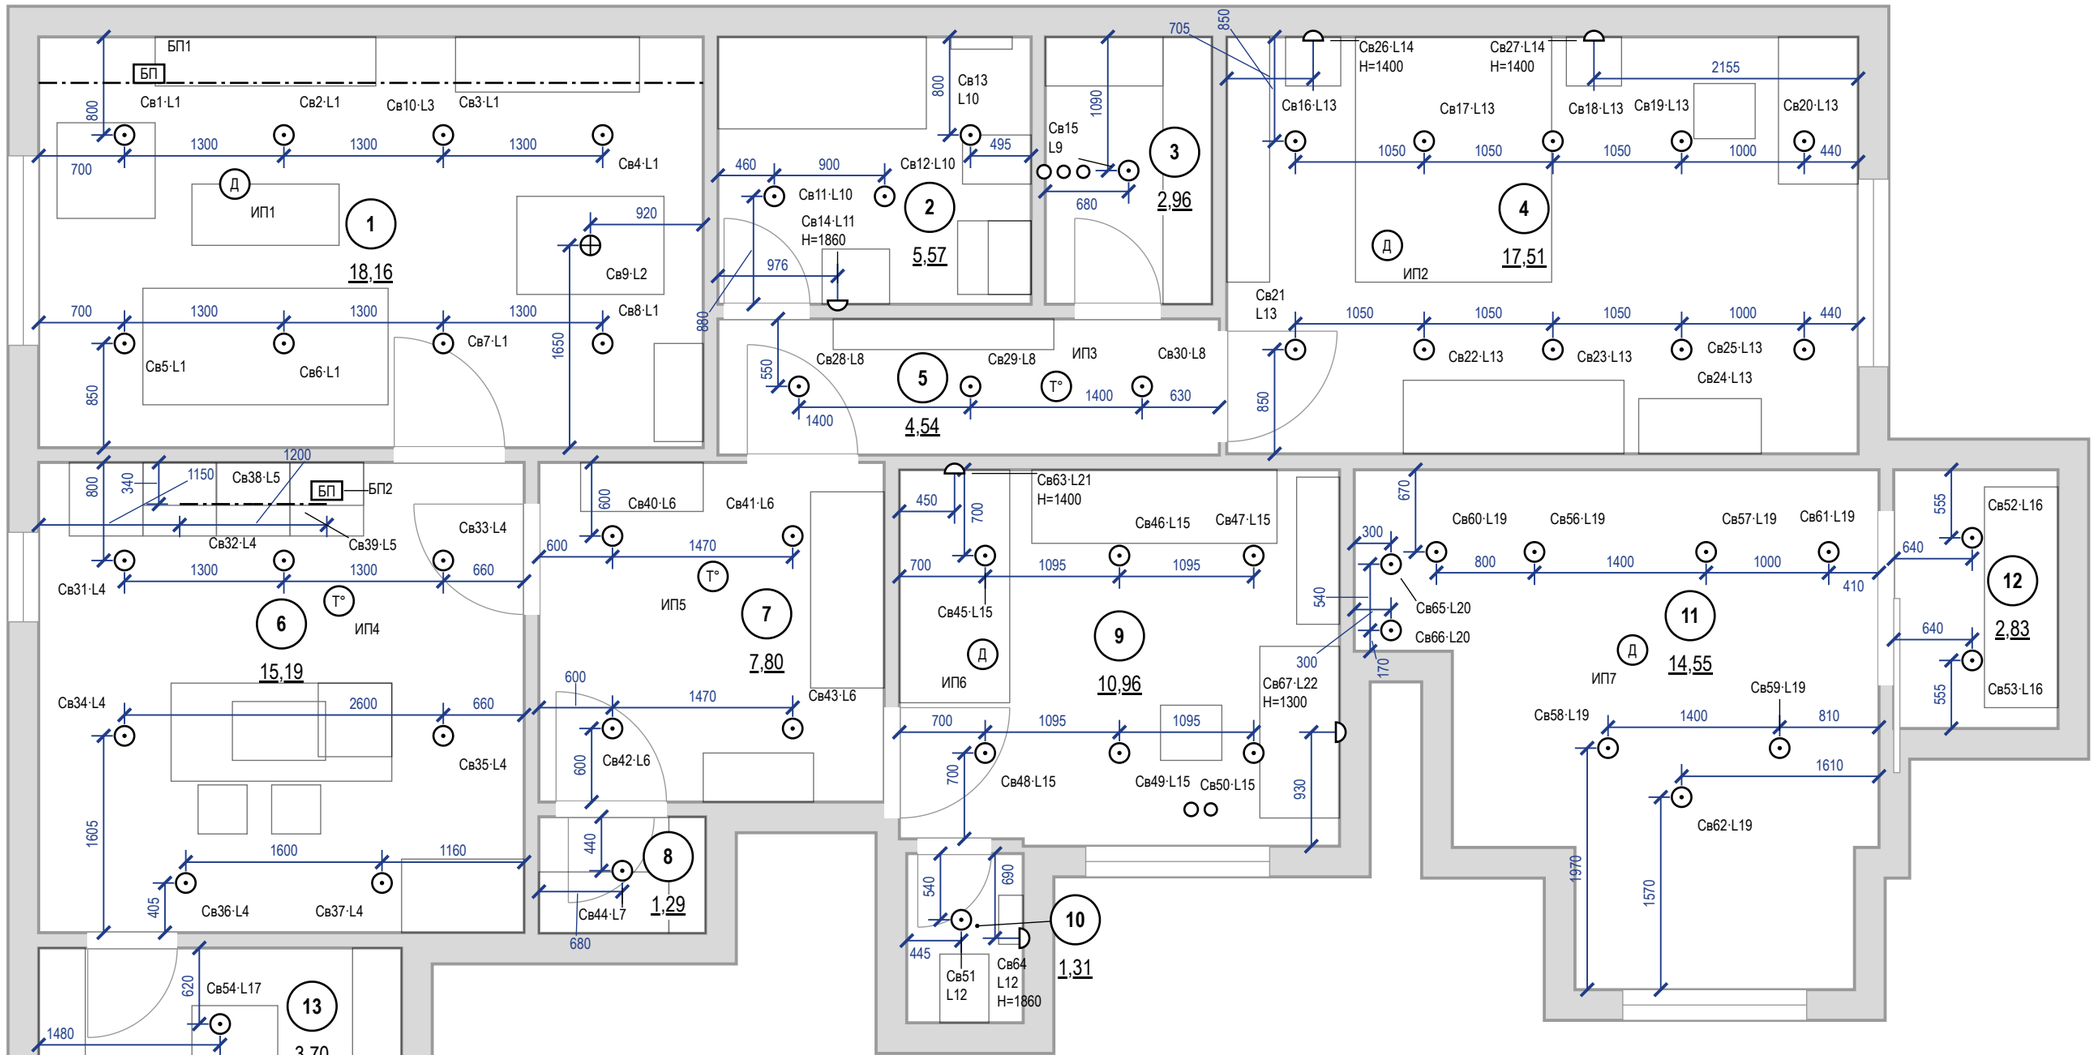

Условные обозначения

- светильник встраиваемый точечный
- светильник подвесной
- светильник настенный (бра), H — высота оси
- светодиодная лента в профиле / в карнизе короба
- Св1·L1 — марка светильника (как в ведомости и на развёртках) · группа включения L (лист 64)
- Д — извещатель пожарный дымовой автономный
- Т° — извещатель пожарный тепловой
- БП — блок питания LED, с доступом (люк от 100×100 мм)
- мебель и сантехприборы — подложка
- стояк: К1 — канализация, В1 — ХВС, Т3 — ГВС
- 1 — номер помещения, площадь м²

Примечания

1. За отметку 0,000 принят уровень чистого пола. Высоты H — от чистого пола до оси изделия; привязки — от чистовой грани стены до оси механизма (у рамки на несколько постов — до оси рамки).
2. Высота установки, не указанная на плане: светильники — на потолке; настенные — по отметке H у знака. Привязки — до оси светильника от чистовой грани стены, по рядам.
3. Во влажных помещениях — светильники не ниже IP44; в зонах 0–2 ванной — по ГОСТ Р 50571.7.701-2024 (зона 1 — IPX5).
4. LED-лента в карнизе подсветки короба — по линии карниза с плана потолков; блок питания — в люке короба (БП на плане), питание ленты длиннее 5 м — с двух концов.
5. Розеточные и мокрые линии — через УЗО или дифавтомат с током утечки не более 30 мА (ПУЭ 7.1.79); в санузле выполнить ДСУП (ПУЭ 7.1.87–7.1.88).
6. Кабель — медный, исполнение нг(A)-LS (ГОСТ 31565-2012); скрытая прокладка только горизонтально и вертикально, фактические трассы зафиксировать исполнительной схемой до закрытия отделкой.
7. Расчёт нагрузок, токов КЗ, селективности и сечений — по проекту ЭОМ организации с допуском СРО; лист задаёт состав, расположение и группы.
8. Ведомость светильников (тип, количество, мощность, поток, Tц, Ra) — лист 63.

	Лист	№ док.	Подпись	Дата	Проект: Четырёхкомнатная квартира	М 1:50
Дизайнер	Кырлан А.С.			14.11.26		
Проверил					План освещения	Стадия П · Лист 62 · Листов 147
Н. контр.						
Утв.						

Параметры светильников для подбора

Поз.	Марки	Наименование	Установка	Кол.	P, Вт	Σ P, Вт	Ф, лм	Тц, К	Ra	Угол, °	IP	Дим.	Слой	Группа	Пом.
1	Св1–Св8, Св16–Св19, Св20, Св21–Св24, Св25, Св31–Св37, Св56–Св62	Встраиваемый точечный	в ГКЛ, корпус ≤ 70 мм	32	12	384	1000	3000	90	—	20	—	общий	L1, L4, L13, L19	1, 4, 6, 11
2	Св9	Подвесной	подвес, низ H=1600	1	15	15	1200	2700	90	—	20	—	рабочий	L2	1
3	Св10	Лента светодиодная 24 В	в карнизе короба, профиль с рассеивателем	5,4 м	9,6/м	52	900/м	2700	90	—	20	да	акцентный	L3	1
4	Св11, Св12, Св13, Св51	Встраиваемый точечный	в ГКЛ, корпус ≤ 70 мм	4	6	24	500	3000	90	—	44	—	общий	L10, L12	2, 10
5	Св14, Св64	Светильник над зеркалом, драйвер встроен	над зеркалом, H=1860	2	8	16	600	3000	90	—	44	—	рабочий	L11, L12	2, 10
6	Св15, Св40–Св44, Св52, Св53, Св65, Св66	Встраиваемый точечный	в ГКЛ, корпус ≤ 70 мм	10	6	60	500	3000	90	—	20	—	общий, акцентный	L6, L7, L9, L16, L20	3, 7, 8, 11, 12
7	Св26, Св27, Св63	Настенный (бра)	на стене, H=1400	3	6	18	400	2700	90	60	20	—	рабочий	L14, L21	4, 9
8	Св28–Св30	Встраиваемый точечный	в ГКЛ, корпус ≤ 70 мм	3	5	15	400	3000	90	—	20	—	общий	L8	5
9	Св38, Св39	Линейный светильник	на поверхности	1,2 м	8	16	700	3000	90	—	20	—	рабочий	L5	6
10	Св45–Св50	Встраиваемый точечный	в ГКЛ, корпус ≤ 70 мм	6	13	78	1100	3000	90	—	20	—	общий	L15	9
11	Св67	Бра подсветки рабочего места, стол М-37	на стене, H=1300	1	7	7	450	3000	90	60	20	—	рабочий	L22	9
12	Св54	Встраиваемый точечный	в ГКЛ, корпус ≤ 70 мм	1	9	9	800	3000	90	—	44	—	общий	L17	13
		Итого		**63 шт + 6,6 м**		**694**									

LED-ленты, линейные светильники и блоки питания

Марка	Пом.	L, м	U, В	Вт/м	Σ P, Вт	БП	P БП, Вт	Загр., %	Питание	Доступ к БП
Св10	1	5,4	24	9,6	52	БП1	100	52	с одного конца	люк 300×300 в коробе потолка у стены А
Св38	6	0,6	24	—	8	БП2	30	53	встроенный ввод	в навесном модуле М-25, съёмная панель
Св39	6	0,6	24	—	8	БП2	30	53	встроенный ввод	в навесном модуле М-25, съёмная панель

Сценарии (помещения со светорегуляторами)

Помещение	Сценарий	Горят группы (уровень)	Управление
1. Зал	Вечер	L2 подвес над обеденным столом — вкл.; L3 лента в карнизе (диммер) — 50 %; остальные выкл.	светорегулятор S2; выключатель S1
	Гости	L1 общий свет (споты) — вкл.; L2 подвес над обеденным столом — вкл.; L3 лента в карнизе (диммер) — 100 %	светорегулятор S2; выключатель S1
	Кино	L3 лента в карнизе (диммер) — 20 %; остальные выкл.	светорегулятор S2
	Уборка	L1 общий свет (споты) — вкл.; L2 подвес над обеденным столом — вкл.; остальные выкл.	выключатель S1

Примечания


1. Позиции и марки Св — те же, что на плане освещения (лист 62); группы L — по плану выключателей (лист 64).
2. Модели светильников не выбраны: лист — техническое задание на подбор. Модель по строке таблицы: поток, Тц, Ra, угол, IP и регулировка яркости не хуже указанных, мощность не больше; встраиваемые — под глубину короба (графа «Установка»). IP 20 — сухие помещения. После выбора моделей (артикул, производитель) лист выпускается как «Спецификация светильников».
3. Длина LED-ленты в карнизе — по линии карниза плана потолков (лист 51); Σ P = Вт/м × длина. Блок питания загружен не больше чем на 80 %; лента 24 В длиннее 10 м питается с двух концов; доступ к блоку питания — люк ревизии 300×300 мм или место, указанное в таблице.
4. Сценарии: % — яркость группы на светорегуляторе; «вкл.» — группа на обычной клавише; группы, не названные в строке, выключены. Светильники и блоки питания групп на светорегуляторе — с регулировкой яркости. Клавиши и светорегуляторы — лист 64.
5. Мощность и поток в таблице — требования к подбору (поток не меньше, мощность не больше указанных); после выбора модели — по её паспорту, Σ P — установленная мощность освещения. Оценка освещённости — на плане освещения; это не светотехнический расчёт.

	Лист	№ док.	Подпись	Дата	Проект: Четырёхкомнатная квартира			
Дизайнер	Кырлан А.С.			14.11.26				
Проверил					Техническое задание на подбор светильников	Стадия	Лист	Листов
Н. контр.						П	63	147
Утв.								

План выключателей (М 1:50)

Условные обозначения

- ⊕ — светильник подвесной
- L1 — группа включения у светильника
- светильник настенный (бра), H — высота оси
- стояк: К1 — канализация, В1 — ХВС, Т3 — ГВС
- светодиодная лента в профиле / в карнизе короба
- (1) — номер помещения, площадь м²

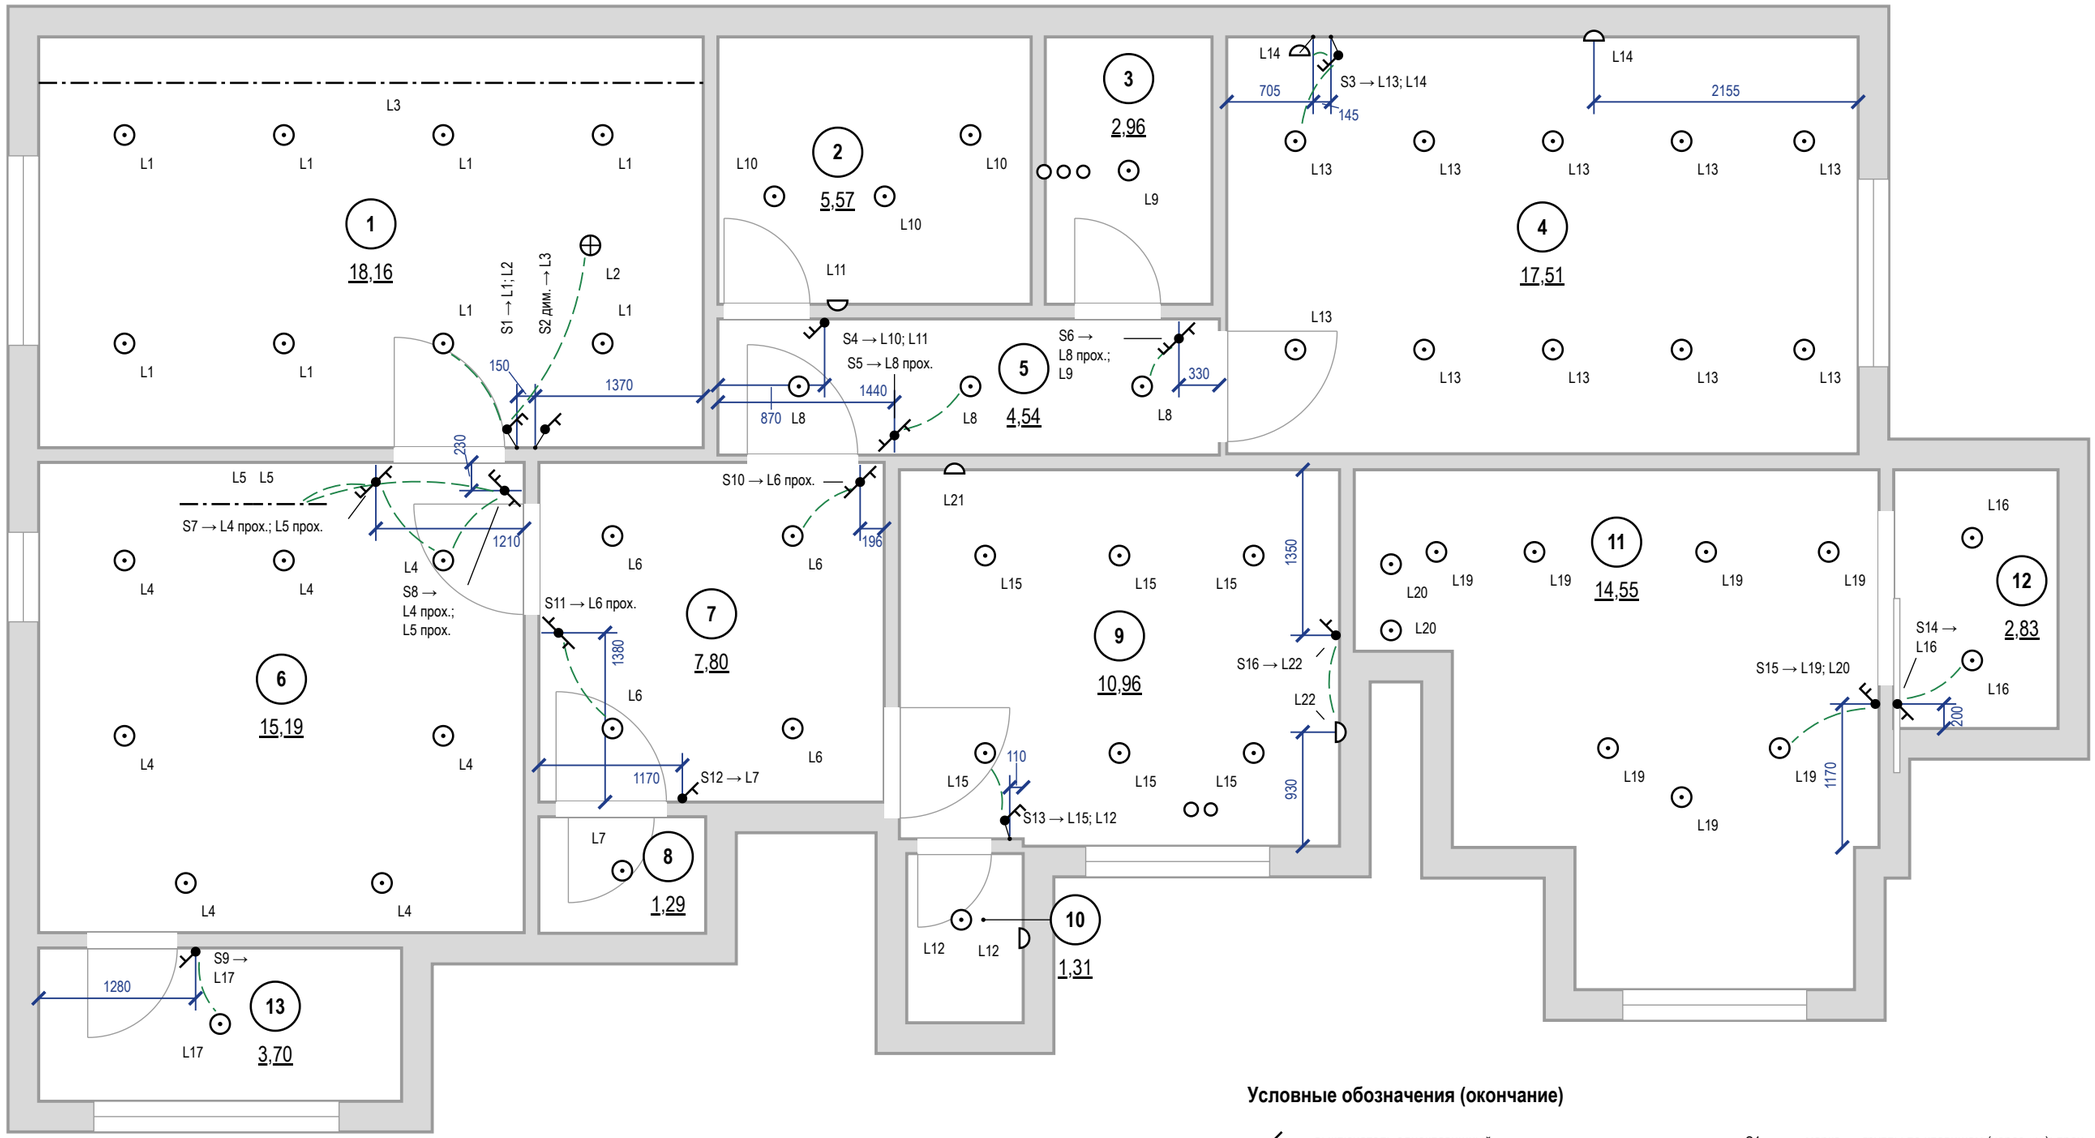

Условные обозначения (окончание)

- выключатель одноклавишный
- выключатель двухклавишный (флажков — по числу клавиш)
- выключатель с проходной или перекрёстной клавишей (обратный флажок); тип клавиши — в подписи
- S1 → — марка → группы по клавишам (через «;»): прох. проходной, перекр. — перекрёстный, дим. светорегулятор; H — высота
- связь: выключатель → ближайший светильник группы в том же помещении (не трасса кабеля); полный состав группы по номеру L
- светильник встраиваемый точечный


Примечания

1. За отметку 0,000 принят уровень чистого пола. Высоты H — от чистого пола до оси изделия; привязки — от чистовой грани стены до оси механизма (у рамки на несколько постов — до оси рамки).
2. Высота установки, не указанная на плане: выключатели — 900 мм от чистого пола (у кровати и другие — H у марки), со стороны дверной ручки (ПУЭ 7.1.51).
3. Какой выключатель какие светильники включает — по номеру группы L: у выключателя (S1 → L1; L2 — клавиши по порядку) и у каждого светильника. Пунктир подсказка к ближайшему светильнику группы в том же помещении (не дальше 3 м), это не трасса кабеля; выключатель за стеной (у двери санузла) и далёкая группа — только номер группы.
4. Группы из нескольких мест (L8 — S5, S6; L4 — S7, S8; L5 — S7, S8; L6 — S10, S11): на крайних местах — проходные клавиши, на промежуточных — перекрёстные; механизмы — в ведомости изделий.
5. Светорегулятор — по заднему фронту (для LED-драйверов), совместимость с драйверами проверить до закупки.
6. Розеточные и мокрые линии — через УЗО или дифавтомат с током утечки не более 30 мА (ПУЭ 7.1.79); в санузле выполнить ДСУП (ПУЭ 7.1.87–7.1.88).
7. Кабель — медный, исполнение нг(A)-LS (ГОСТ 31565-2012); скрытая прокладка только горизонтально и вертикально, фактические трассы зафиксировать исполнительной схемой до закрытия отделкой.
8. Расчёт нагрузок, токов КЗ, селективности и сечений — по проекту ЭОМ организации с допуском СРО; лист задаёт состав, расположение и группы.
9. Группы без выключателя: L21 — выключатель в исходных данных не задан; управление группой согласуется до монтажа.

	Лист	№ док.	Подпись	Дата	Проект: Четырёхкомнатная квартира			М 1:50
Дизайнер	Кырлан А.С.			14.11.26	Управление светильниками	Стадия	Лист	Листов
Проверил						П	64	147
Н. контр.								
Утв.								

выпуск 14.11.2026 № e7147312ff · стр. 64 из 147

План вентиляции (М 1:75)

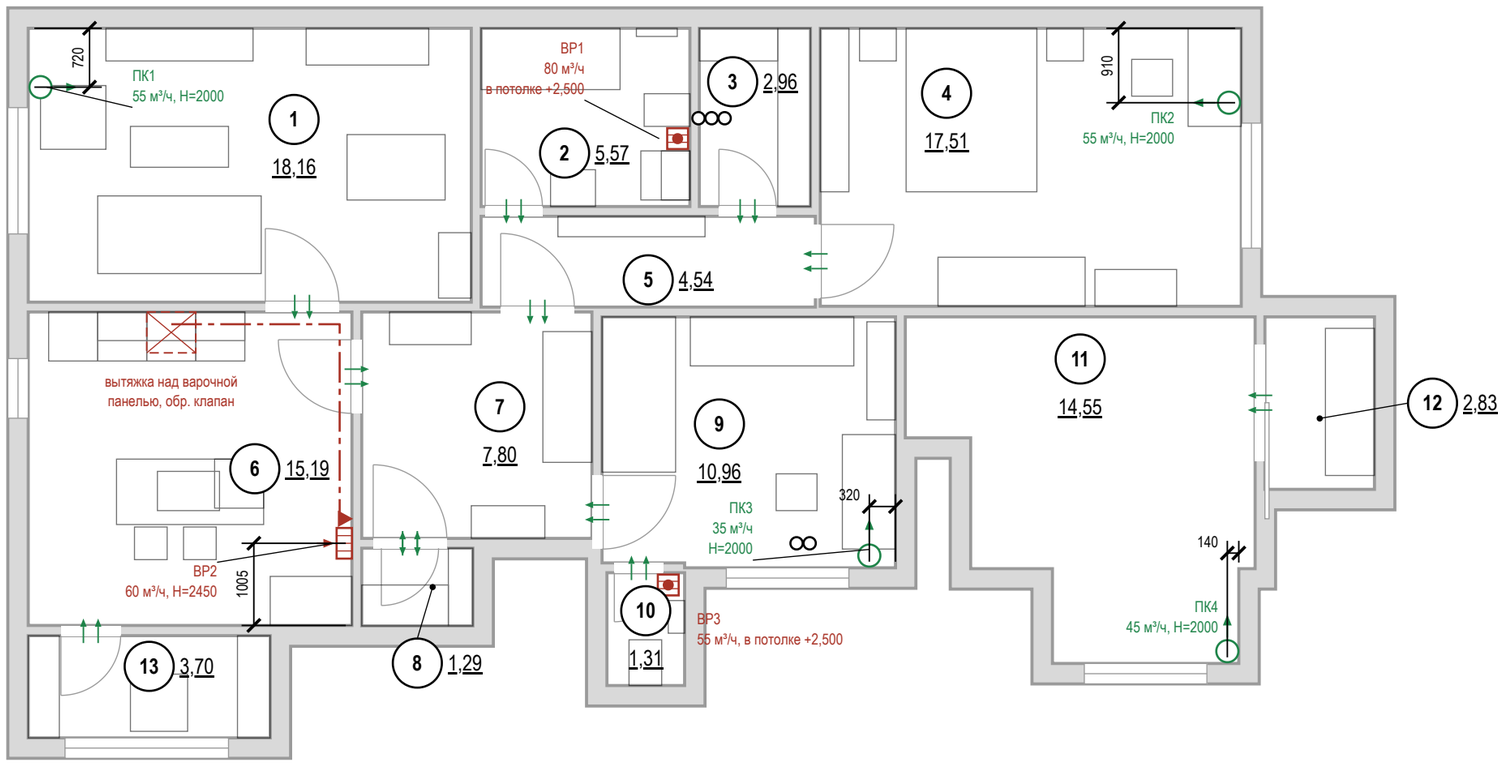

Условные обозначения

- стояк: К1 — канализация, В1 — ХВС, Т3 — ГВС
- номер помещения, площадь м²
- вытяжная решётка в вентканал: марка, расход м³/ч, Н центра от чистого пола
- вентилятор с обратным клапаном в подшивном потолке, воздуховод за потолком до канала
- приточный клапан (КИВ) в наружной стене: марка, расход, Н центра
- переток: зазор под полотном или переточная решётка
- кухонная вытяжка над варочной панелью
- воздуховод кухонной вытяжки в коробе под потолком
- отдельный вход воздуховода в вентканал, обратный клапан

Воздухообмен, м³/ч

№	Помещение	Выт. норма	Выт. проект	Прит. норма	Прит. проект	Устрой-ства
1	Зал			55	55	ПК1
2	Ванная комната	50	80			ВР1
3	Тёмная комната	2				переток
4	Детская 1			53	55	ПК2
6	Кухня	60	60			ВР2
8	Гардеробная 2	1				переток
9	Детская 2			33	35	ПК3
10	Санузел	25	55			ВР3
11	Гостиная			44	45	ПК4
12	Гардеробная 1	2				переток
	Итого	**140**	**195**	**185**	**190**	

Воздухообмен квартиры — по большей из сумм притока и вытяжки: норма 185 м³/ч, проект 195 м³/ч.
Вытяжка не меньше притока — баланс сведён.


Привязки — до обмера
Вентканалы в исходных данных не заданы: решётки и вход вытяжки показаны у стояков К1 (вентблок у мокрой зоны). До черновых работ — обмер каналов и проверка тяги; лист перевыпустить по факту.

Примечания

1. Расчёт систем ОВ и подбор оборудования — проектная организация с допуском СРО; лист даёт места, трассы и привязки.
2. Нормы вытяжки — СП 54.13330.2022 (Изм. 1, 2), табл. 7.1: кухня с электроплитой 60 м³/ч, с газовой 100; ванная и совмещённый санузел 50; уборная 25; гардеробная 0,2 ч⁻¹. Приток в жилые — 3 м³/ч на 1 м² (менее 20 м² общей площади на человека), иначе 30 м³/ч на человека.
3. Вентканалы и шахты не сужать, не переносить и не закрывать; вентилятор и кухонная вытяжка — через обратный клапан, без перекрытия естественной тяги.
4. Проектные расходы — не ниже нормы, вытяжка сведена с притоком вентиляторами мокрых помещений. Клапаны — в простенке у окна, центр 2000 мм, не над кроватью, не ближе 300 мм к стоякам отопления; типоразмер — на расход.
5. Под подшивным потолком вытяжка — в потолке, воздуховодом за потолком до канала. Кухонная вытяжка в воздухообмен не включена: воздуховод не менее Ø125 в коробе, вход в канал отдельный.
6. Переток — зазор под полотнами межкомнатных дверей или переточная решётка.
7. Кондиционирование заданием не предусмотрено; при установке трассы фреона и дренажа (не менее 40 мм/м, в К1 через сифон) и питание заложить до черновых работ.
8. Привязки оборудования — по паспортам приобретённых моделей, до черновых работ.

	Лист	№ док.	Подпись	Дата	Проект: Четырёхкомнатная квартира	М 1:75		
Дизайнер	Кырлан А.С.			14.11.26				
Проверил					План вентиляции	Стадия	Лист	Листов
Н. контр.						П	65	147
Утв.								

План отопления (М 1:50)

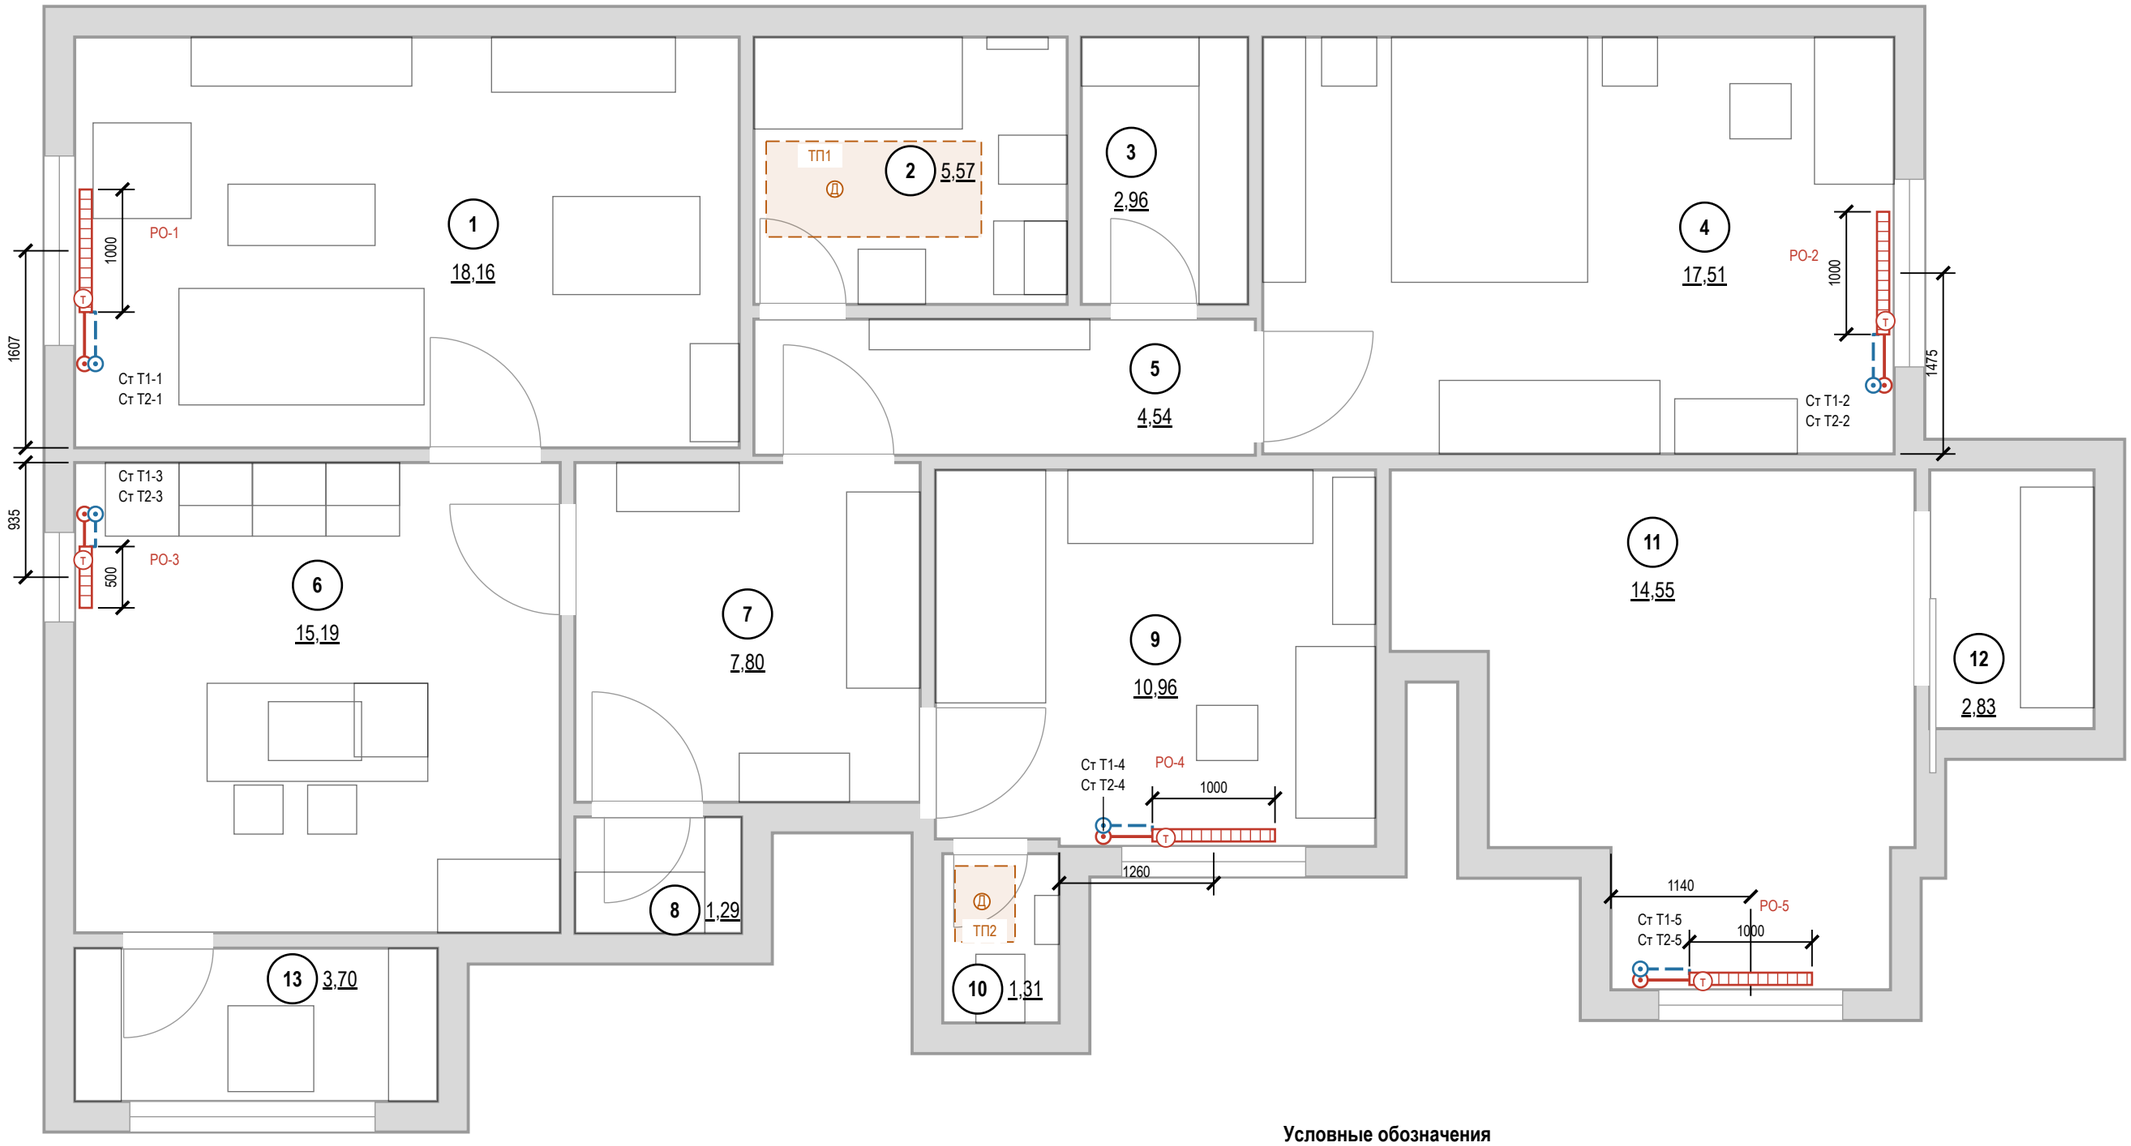

Примечания

1. Расчёт системы отопления, теплопотерь и подбор приборов — проектная организация с допуском СРО; лист даёт места и привязки.
2. Электрический тёплый пол: ТП1 — пом. 2, мат 1755×780 мм, 205 Вт; ТП2 — пом. 10, мат 490×620 мм, 50 Вт; контуры показаны пунктиром; датчик температуры (Д) — в гофротрубе, трасса к терморегулятору — по обмеру. Марка мата и точное положение датчика — при закупке и по обмеру.
3. Тип, длина и мощность радиаторов — по теплотехническому расчёту; лист задаёт места, зазоры и подключение.
4. Радиаторы — под каждым окном жилых комнат и кухни, центр по оси проёма, длина 0,7 ширины окна (кратно 100); окончательно — по расчёту.
5. Зазоры радиатора: низ не менее 100 мм от чистого пола, верх не менее 100 мм до подоконника, 30–50 мм от стены до задней панели; центр по оси окна с допуском ±20 мм. Верх до подоконника — 180 мм.
6. Радиаторы не закрывать глухими коробами и мебелью; перенос и замена приборов в многоквартирном доме — переустройство, согласование с управляющей организацией (ЖК РФ ст. 25–26); вынос на лоджию запрещён.
7. Трубы отопления через межквартирные стены не прокладывать (СП 51.13330.2011, п. 9.19); через перекрытия и перегородки — в гильзах.
8. Привязки приборов и подводок — по паспортам приобретённых радиаторов и клапанов, до черновых работ.
9. Привязки — до обмера: Стояки отопления в исходных данных не заданы: показаны у откосов окон, подводки — принципиально. До черновых работ обмер стояков и паспорта приборов; лист перевыпустить по факту.
10. До закрытия отделкой трубопроводы отопления испытать гидростатическим давлением с оформлением акта (СП 73.13330.2016, 7.2–7.3).

Условные обозначения

- 1 — номер помещения, площадь м²
- радиатор отопления (марка РО-N, длина по плану)
- Т — клапан с термоголовкой на подаче
- стояк отопления, подающий (Ст Т1-N)
- стояк отопления, обратный (Ст Т2-N)
- Т1 — отопление, подающий трубопровод
- Т2 — отопление, обратный трубопровод


	Лист	№ док.	Подпись	Дата	Проект: Четырёхкомнатная квартира			М 1:50
Дизайнер	Кырлан А.С.			14.11.26	План отопления	Стадия	Лист	Листов
Проверил						П	66	147
Н. контр.								
Утв.								

Спецификация плинтусов

Наименование	Помещения	Длина, м (с запасом)
Плинтус МДФ под окраску 80×16 мм, крепление к стене, окраска в цвет Tikkurila F497	1, 3, 4, 6, 8, 9, 11, 12	99
Плинтус МДФ под окраску 80×16 мм, крепление к стене, окраска в цвет Tikkurila J484	5, 7	19
Плинтус из керамогранита пола, подрезка 80 мм, верхняя кромка с запилом 45°, h = 80 мм, крепление к стене	13	9

Отметки по высоте





±0,000	чистый пол пом. 1, 3–9, 11, 12; отсчёт высот
−0,015	чистый пол пом. 2, 10, ниже на 15 мм
−0,030	чистый пол пом. 13, ниже на 30 мм
−0,170	верх плиты — расчёт, не замер (задание на обмер)
сущ. пол	снимается до плиты; не замерен (задание на обмер)

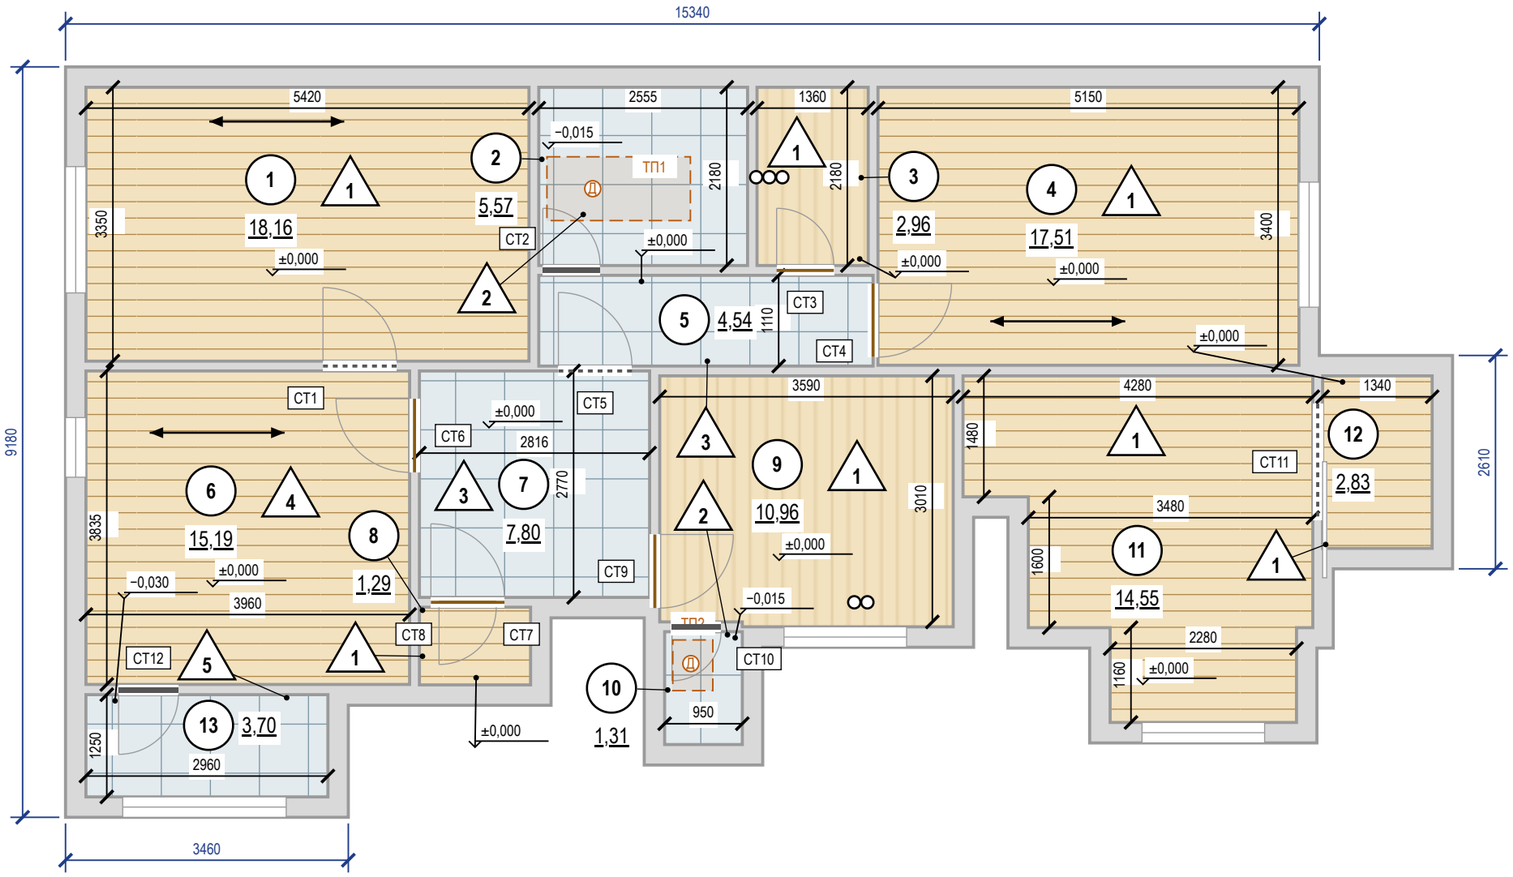

Примечания

1. За отметку ±0,000 принят чистый пол, не существующий (блок отметок). Площади — по чистым размерам помещений, м²; размеры — в мм.
2. Стык разнотипных покрытий — по оси дверного полотна (под полотном в закрытом положении); решение стыка — по ведомости стыков.
3. Размеры помещений в свету (ширина × длина, мм), не поместившиеся на плане: пом. 5 — 4090 × 1110; пом. 8 — 1360 × 950; пом. 9 — 3590 × 3010, 2580 × 60; пом. 10 — 950 × 1380; пом. 12 — 1340 × 2110.
4. Пол санузлов ниже смежных помещений на 15 мм за счёт меньшей толщины стяжки (верх плиты общий — по экспликации полов); гидроизоляция по стяжке с заведением на стены не менее 200 мм (СП 29.13330.2011, п. 7.2), до облицовки — тест проливом и акт скрытых работ.
5. Выпуски канализации с уклоном и трассы водоснабжения — в слое засыпки под стяжкой (по экспликации полов); отметки, уклоны и прочистки — по листу разводки ВК 40.
6. Штучные покрытия (инженерная доска): направление — по стрелке; влажность основания по СМ не более 2,0 % (по ТУ изготовителя).
7. Ровность основания — просвет под 2-метровой рейкой не более 2 мм: пом. 1, 3, 4, 6, 8, 9, 11, 12 (инженерная доска), пом. 2, 5, 7, 10 (керамогранит); 3 мм: пом. 13 (керамогранит); проверить до укладки покрытия (СП 71.13330.2017, табл. 8.5).
8. Плавающая стяжка по звукоизоляции: демпферная (кромочная) лента по контуру помещения, у стояков и колонн — до верха чистого пола (СП 51.13330.2011, п. 9.11); плинтус крепится только к стене.
9. Сетка на плитке — условная, в размер формата; точка старта и раскладка — по листу раскладки плитки.
10. Узор покрытия (заливка-код типа пола) прерывается под надписями — площадями помещений и отметками чистого пола.
11. Электрический тёплый пол: ТП1 — пом. 2, мат 1755×780 мм, 205 Вт; ТП2 — пом. 10, мат 490×620 мм, 50 Вт; контуры показаны пунктиром; датчик температуры (Д) — в гофротрубе, трасса к терморегулятору — по обмеру. Марка мата и точное положение датчика — при закупке и по обмеру.
12. Пироги полов — по экспликации полов: слои сверху вниз, толщины в мм; гидроизоляция мокрых зон — в пироге и в ведомости отделки; схема пола — без масштаба.

Экспликация полов

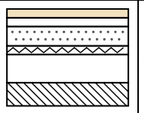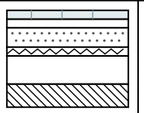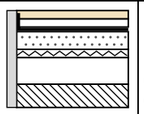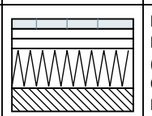Номер помещения	Тип пола	Схема пола	Данные элементов пола (наименование, толщина, основание), мм	Площадь, м²
1, 3, 4, 8, 9, 11, 12	1		Инженерная доска дуб на клею — 14 Клей паркетный МС-полимерный — 1 Стяжка ЦПС М300 (В22,5), фибра, по звукоизоляции — 55 Звукоизоляция — минплита 110 кг/м³ 20 Засыпка керамзитовая фр. 0–5, уплотнённая — 80 Плита перекрытия монолитная Всего 170 мм; ЧП ±0,000, верх плиты −0,170	68,26
2, 10	2		Керамогранит 600×600×10 — 10 Нагревательный мат в слое клея С2 TE S1 — 8 Гидроизоляция обмазочная, 2 слоя (заход на стены — по ведомости отделки) — 2 Сборное основание ГВЛВ 2×12,5 — 25 Засыпка керамзитовая сухая фр. 0–5 (в слое — выпуски К1) — 110 Плита перекрытия монолитная Всего 155 мм; ЧП −0,015, верх плиты −0,170	6,88
5, 7	3		Керамогранит 600×600×10 — 10 Клей плиточный С2 TE S1 — 5 Стяжка ЦПС М300 (В22,5), фибра, по звукоизоляции — 55 Звукоизоляция — минплита 110 кг/м³ 20 Засыпка керамзитовая фр. 0–5, уплотнённая — 80 Плита перекрытия монолитная Всего 170 мм; ЧП ±0,000, верх плиты −0,170	12,34
6	4		Инженерная доска дуб на клею — 14 Клей паркетный МС-полимерный — 1 Гидроизоляция полиуретановая, 2 слоя (зона мойки и острова) — 2 Стяжка ЦПС М300 (В22,5), фибра, по звукоизоляции — 53 Звукоизоляция — минплита 110 кг/м³ 20 Засыпка керамзитовая фр. 0–5, уплотнённая — 80 Плита перекрытия монолитная Всего 170 мм; ЧП ±0,000, верх плиты −0,170	15,19
13	5		Керамогранит 600×600×10 — 10 Клей плиточный С2 TE S1 (деформируемый) — 5 Сборное основание ГВЛВ 2×12,5 — 25 Пенополистирол экструзионный 2×50 100 Плита перекрытия монолитная Всего 140 мм; ЧП −0,030, верх плиты −0,170	3,70
			Итого	**106,37**

	Лист	№ док.	Подпись	Дата
Дизайнер	Кырлан А.С.			14.11.26
Проверил				
Н. контр.				
Утв.				


Проект: Четырёхкомнатная квартира — **М 1:75**

План покрытий пола


Стадия	Лист	Листов
П	67	147

выпуск 14.11.2026 № e7147312ff · стр. 67 из 147


Фрагмент 1. Ванная комната (пом. 2). Пол 600×600, шов 2 мм (М 1:50)

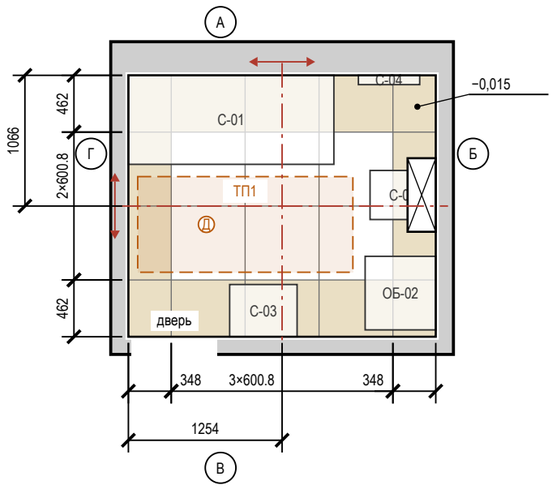


Фрагмент 2. Коридор (пом. 5). Пол 600×600, шов 2 мм (М 1:50)

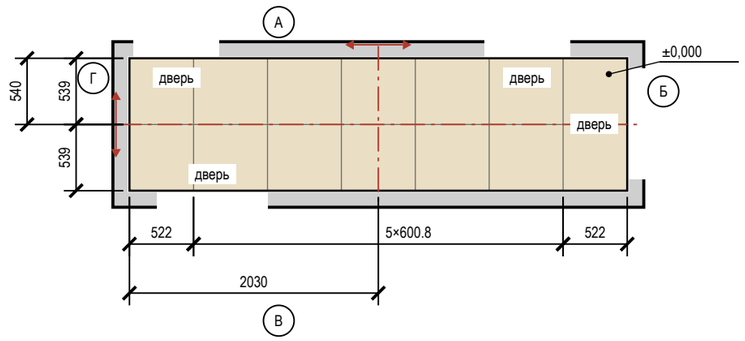

Фрагмент 3. Прихожая-коридор (пом. 7). Пол 600×600, шов 2 мм (М 1:50)

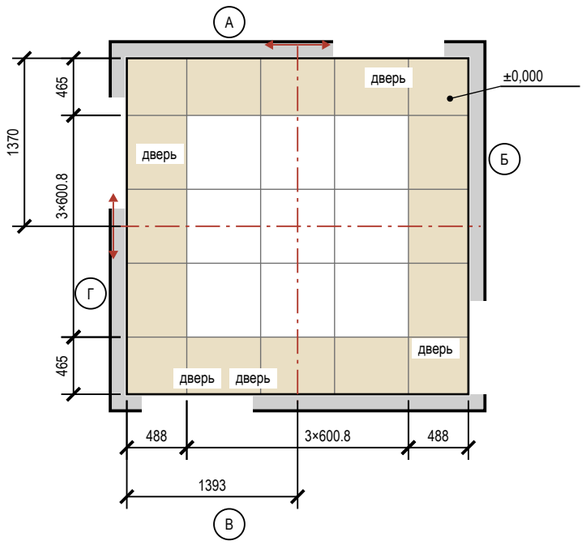

Фрагмент 4. Санузел (пом. 10). Пол 600×600, шов 2 мм (М 1:50)

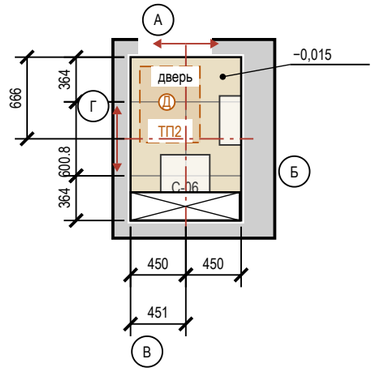

Ведомость материалов

Материал	Класс, код	Норма расхода	Кол-во
Затирка	CG2WA аналог: Mapei Ultracolor 133	(a+b)/ab·шов·t·1,6	5,6 кг
Затирка	CG2WA	(a+b)/ab·шов·t·1,6	0,1 кг
Клей	C2 TE S1 аналог: Litokol K80 Eco	1,2 кг/м²·мм, слой 5	340 кг (14 меш.)
Клей	C2 TE S1	1,2 кг/м²·мм, слой 5	8 кг (1 меш.)
Гидроизоляция	обмазочная, 2 слоя: пол, стены по периметру и зоны замачивания	по ТУ	16,2 м²
Демпф. лента	по периметру пола из плитки		29,1 м

Ведомость плитки

Помещение, поверхность	Плитка, код	Формат	Шов	S, м²	Целых	Подр.	С запасом
Ванная комната, пол	керамогранит матовый R10, тон J484	600.8×600.8	2	5,57	6	14	22
Ванная комната, стены А–Г	керамогранит матовый, тон F497	600.8×600.8	2	21,66	23	67	100
Ванная комната, короб инсталляции	керамогранит матовый, тон F497	600.8×600.8	2	1,36	1	6	8
Коридор, пол	керамогранит матовый R10, тон V486	600.8×600.8	2	4,54	0	14	16
Прихожая-коридор, пол	керамогранит матовый R10, тон V486	600.8×600.8	2	7,80	9	16	28
Санузел, пол	керамогранит матовый R10, тон J484	600.8×600.8	2	1,31	0	6	7
Санузел, стены А–Г	керамогранит матовый, тон F497	600.8×600.8	2	9,44	6	44	56
Санузел, короб инсталляции	керамогранит матовый, тон F497	600.8×600.8	2	1,76	0	10	11
Кухня, фартук (ст. А)	аналог: керамогранит матовый, тон F497	600.8×600.8	2	1,11	1	3	5
Итого 600.8×600.8				**54,54**	**46**	**180**	**253**

Условные обозначения

- плитка целая; тонкая линия — шов
- плитка с подрезкой (размер — на цепочке)
- ось старта; стрелки — направление укладки
- сантехприбор: габарит, высота по практике
- короб инсталляции: плитка пола — до короба
- электрический тёплый пол: контур мата ТП, Д — датчик
- отметка чистого пола на полке выноски, м
- А — обозначение стены А–Г (как на развёртках)


Примечания

1. Раскладка от чистовых размеров: стены санузлов теряют 10 + 5 + 9 = 24 мм на сторону (штукатурка, клей, плитка); подрезки — чистые, без шва.
2. Старт — от центра помещения (штрихпунктир, стрелки — направление укладки); размер старта — от чистовых стен Г и А.
3. Раскладка фартука «Кухня» — на листе «Раскладка плитки. Фартук кухни».
4. Количество: целые по раскладке + по одной на подрезку, запас 10 %; один артикул — одна партия и тон. Исключены поддон, короб, проёмы и места за коробом; S — по чистым граням: стены нетто = зона облицовки по ведомости отделки − место за коробом инсталляции 1,71 м² (плитку за коробом не кладут), короб — отдельной строкой.
5. Клей C2 TE S1 аналог: Litokol K80 Eco; C2 TE S1 (ГОСТ Р 56387-2018), затирка CG2WA аналог: Mapei Ultracolor 133; CG2WA; расход — по ТУ выбранной марки.
6. Гидроизоляция: пол и стены 200 мм от ЧП; над ванной — до 2100 и 300 мм за борт (пом. 2) (см. развёртки); акт скрытых работ, пролив 24 ч.
7. Электрический тёплый пол: ТП1 — пом. 2, мат 1755×780 мм, 205 Вт; ТП2 — пом. 10, мат 490×620 мм, 50 Вт; контуры показаны пунктиром; датчик температуры (Д) — в гофротрубе, трасса к терморегулятору — по обмеру. Марка мата и точное положение датчика — при закупке и по обмеру. Плитку над матом клеить клеем, который изготовитель допускает для тёплого пола, до включения выдержать срок по ТУ клея.
8. Швы пола совмещены со швами стены А; по периметру — демпферная лента.
9. Отметка чистого пола −0,015, порог 15 мм; стык с соседним покрытием — по оси полотна двери.

	Лист	№ док.	Подпись	Дата	Проект: Четырёхкомнатная квартира			М 1:50
Дизайнер	Кырлан А.С.			14.11.26	Раскладка плитки. Планы полов	Стадия	Лист	Листов
Проверил						П	68	147
Н. контр.								
Утв.								

выпуск 14.11.2026 № e7147312ff · стр. 68 из 147

Фрагмент 1. Кухня (пом. 6), фартук, стена А. 600×600, шов 2 мм (М 1:20)

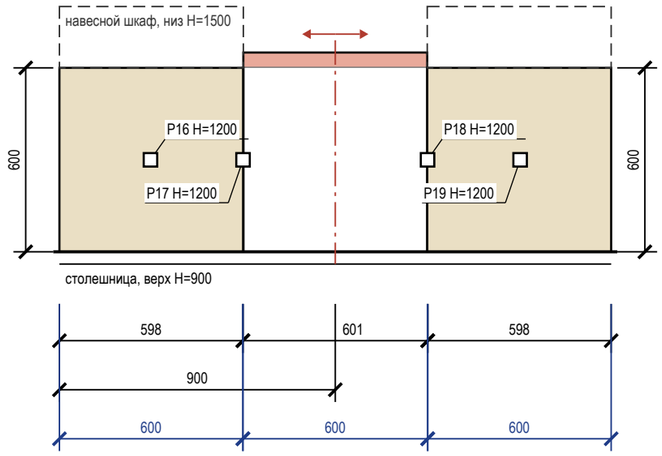

Условные обозначения

- плитка целая; тонкая линия — шов
- плитка с подрезкой (размер — на цепочке)
- ось старта; стрелки — направление укладки
- электроточка: марка и Н — по листам ЭОМ
- столешница (верх)
- навесной шкаф над фартуком

Подсчёт плитки

Поверхность	Формат	S, м²	Целых	Подр.	С запасом
Кухня, фартук (ст. А)	600×600	1,11	1	3	5


Примечания

1. Фартук, Кухня: 600×600 горизонтально, шов 2 мм; зоны 600 мм — 900…1500, 600 мм — 900…1550, 600 мм — 900…1500 (от столешницы до низа навесного шкафа, без шкафа — 650 мм). Старт от центра участка, подрезки 598 мм. Площадь 1,11 м² — как в ведомости отделки.
2. Фартук — после монтажа столешницы, низ на 2–3 мм выше неё, шов со столешницей — санитарный герметик; навесные шкафы — после фартука. Торцы у пенала и стены — профиль или запил 45°.
3. Фартук, Кухня: в зоне до отм. 1550 верхний ряд подрезан 47 мм — меньше 1/3 плитки; полоса прикрыта корпусом навесного модуля и на виду не остаётся. Раскладкой не снимается: убрать подрезку можно, только выровняв низ этого модуля с соседними (1500 мм) — решение мебельщика.
4. Клей, затирка и итог по форматам — в ведомостях листа «Раскладка плитки. Планы полов».

	Лист	№ док.	Подпись	Дата	Проект: Четырёхкомнатная квартира			М 1:20
Дизайнер	Кырлан А.С.			14.11.26	Раскладка плитки. Фартук кухни	Стадия	Лист	Листов
Проверил						П	69	147
Н. контр.								
Утв.								

выпуск 14.11.2026 № e7147312ff · стр. 69 из 147


Стена А (М 1:25)

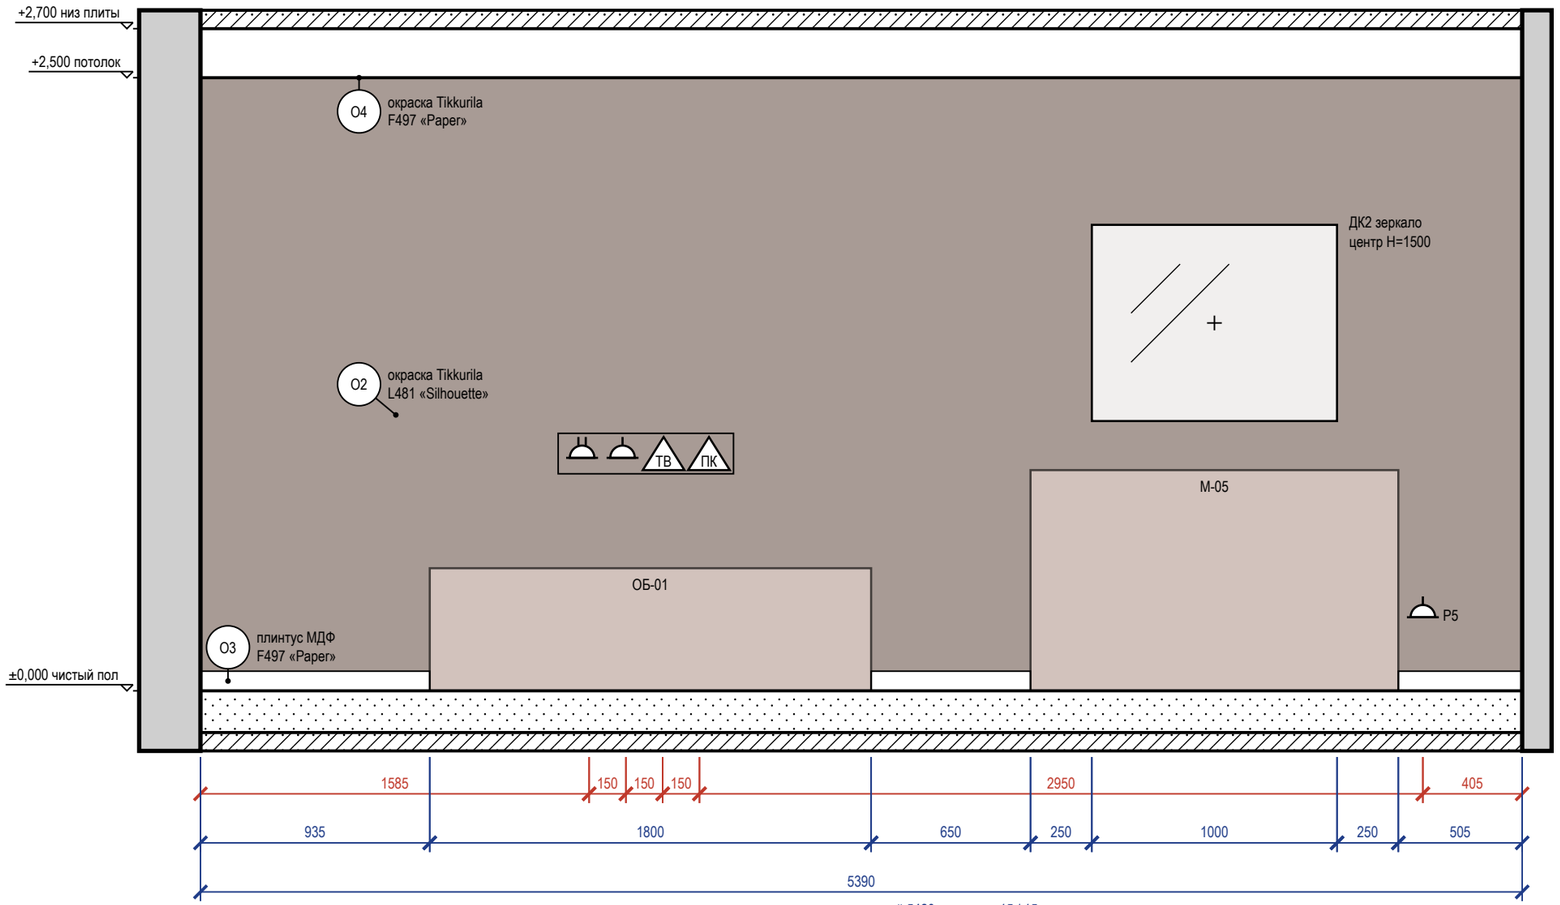

Стена А — визуализация, лист 3



Схема развёрток (М 1:50)

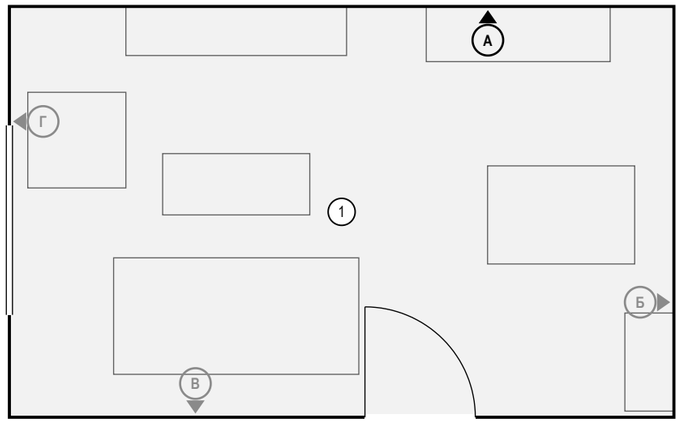

Ведомость точек и выводов

Марка	Что это	Гр.	H, мм	От угла, мм	Примечание
Р1	розетка: ТВ-зона: телевизор, медиаплеер	5	950	1585	рамка 2 поста
Р2	розетка: ТВ-зона: саундбар	5	950	1735	
ТВ1	розетка ТВ: ТВ-зона		950	1885	
LAN1	розетка RJ45: ТВ-зона		950	2035	
Р5	розетка: обеденная зона, буфет М-05	5	300	4985	

Ведомость изделий и проёмов (на листе)

Марка	Изделие, проём	На виде Ш×В, мм	Низ, мм
ОБ-01	ТВ-тумба с экраном 55"	1800×500	0
М-05	буфет обеденной зоны	1500×900	0
ДК2	зеркало	1000×800	1100

Ведомость отделки (на листе)

Марка	Поверхность	Материал, изделие	Цвет, код	Кол.
О2	акцентная стена	окраска, Tikkurila Optiva 5 Matt, аналог: интерьерная краска, класс 2 по EN 13300, глубокоматовая/матовая, база С, матовая, подготовка К3	Tikkurila L481 «Silhouette»	13,5 м²
О3	плинтус	плинтус МДФ, h 80 мм, аналог: плинтус МДФ под окраску 80×16 мм, полуглянцевая	Tikkurila F497 «Paper»	2,1 м
О4	потолок	окраска, Tikkurila Anti-Reflex 2, глубокоматовая, подготовка Q3	Tikkurila F497 «Paper»	18,2 м²


Примечания

1. Размеры — в мм от чистовых поверхностей стен; условные обозначения и общие указания — лист 19.
2. Картины и зеркала крепить к основанию по паспорту изделия (закладные и анкеры — в перечне скрытых работ); крест — ось центра предмета.
3. Потолок — у каждой стены свой, по плану потолков (ПТ1); ступени — зоной, кромка короба перед нишей — тонкой линией; в поле потолка: ПТ2 +2,600.
4. Часть марок не уместилась у знаков: коды, высоты и привязки этих позиций — в ведомости точек и выводов под видами.


	Лист	№ док.	Подпись	Дата	Проект: Четырёхкомнатная квартира	М 1:25		
Дизайнер	Кырлан А.С.			14.11.26				
Проверил					Развёртка стены А. Зал (пом. 1)	Стадия	Лист	Листов
Н. контр.						П	70	147
Утв.								

выпуск 14.11.2026 № e7147312ff · стр. 70 из 147

Стена Б (М 1:20)

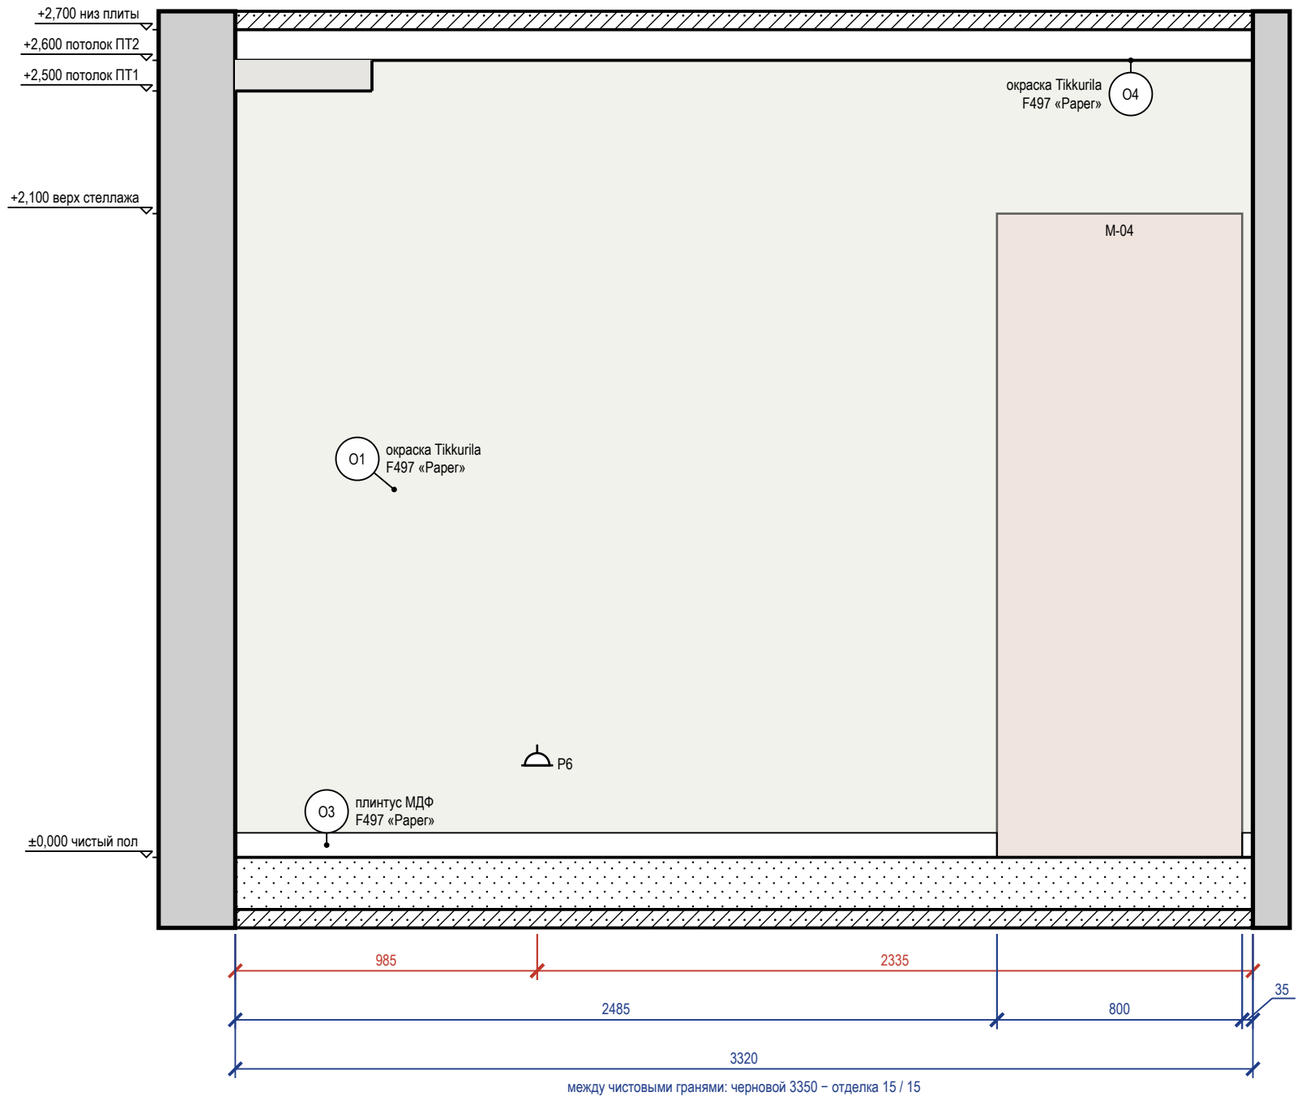


Стена Б — визуализация, лист 4

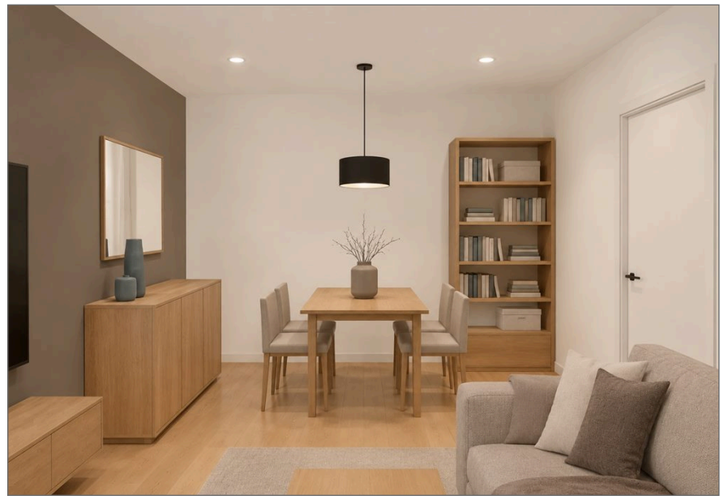

Ведомость отделки (на листе)

Марка	Поверхность	Материал, изделие	Цвет, код	Кол.
O1	стены	окраска, Tikkurila Optiva 5 Matt, матовая, подготовка К3	Tikkurila F497 «Paper»	8,6 м²
O3	плинтус	плинтус МДФ, h 80 мм, аналог: плинтус МДФ под окраску 80×16 мм, полуглянцевая	Tikkurila F497 «Paper»	2,5 м
O4	потолок	окраска, Tikkurila Anti-Reflex 2, глубокоматовая, подготовка Q3	Tikkurila F497 «Paper»	18,2 м²

Схема развёрток (М 1:50)

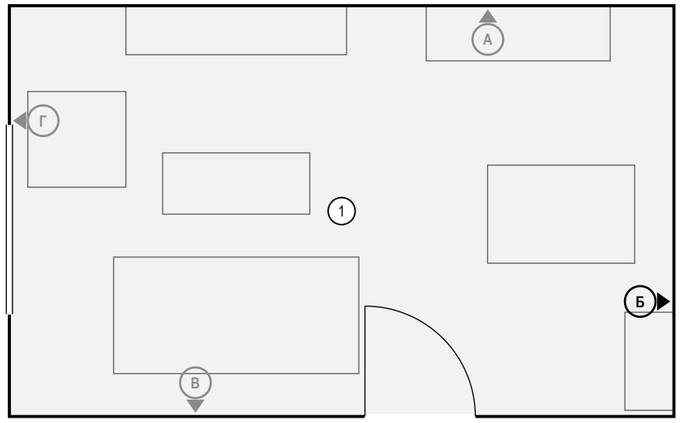

Ведомость точек и выводов

Марка	Что это	Гр.	Н, мм	От угла, мм	Примечание
P6	розетка: уборка	5	300	985	

Ведомость изделий и проёмов (на листе)

Марка	Изделие, проём	На виде Ш×В, мм	Низ, мм
M-04	стеллаж-витрина	800×2100	0

Примечания

1. Размеры — в мм от чистовых поверхностей стен; условные обозначения и общие указания — лист 19.
2. Потолок — у каждой стены свой, по плану потолков (ПТ2, ПТ1); ступени — зоной, кромка короба перед нишей — тонкой линией.

	Лист	№ док.	Подпись	Дата
Дизайнер	Кырлан А.С.			14.11.26
Проверил				
Н. контр.				
Утв.				

Проект: Четырёхкомнатная квартира — М 1:20

Развёртка стены Б. Зал (пом. 1)

Стадия	Лист	Листов
П	71	147

выпуск 14.11.2026 № e7147312ff · стр. 71 из 147

Стена В (М 1:25)


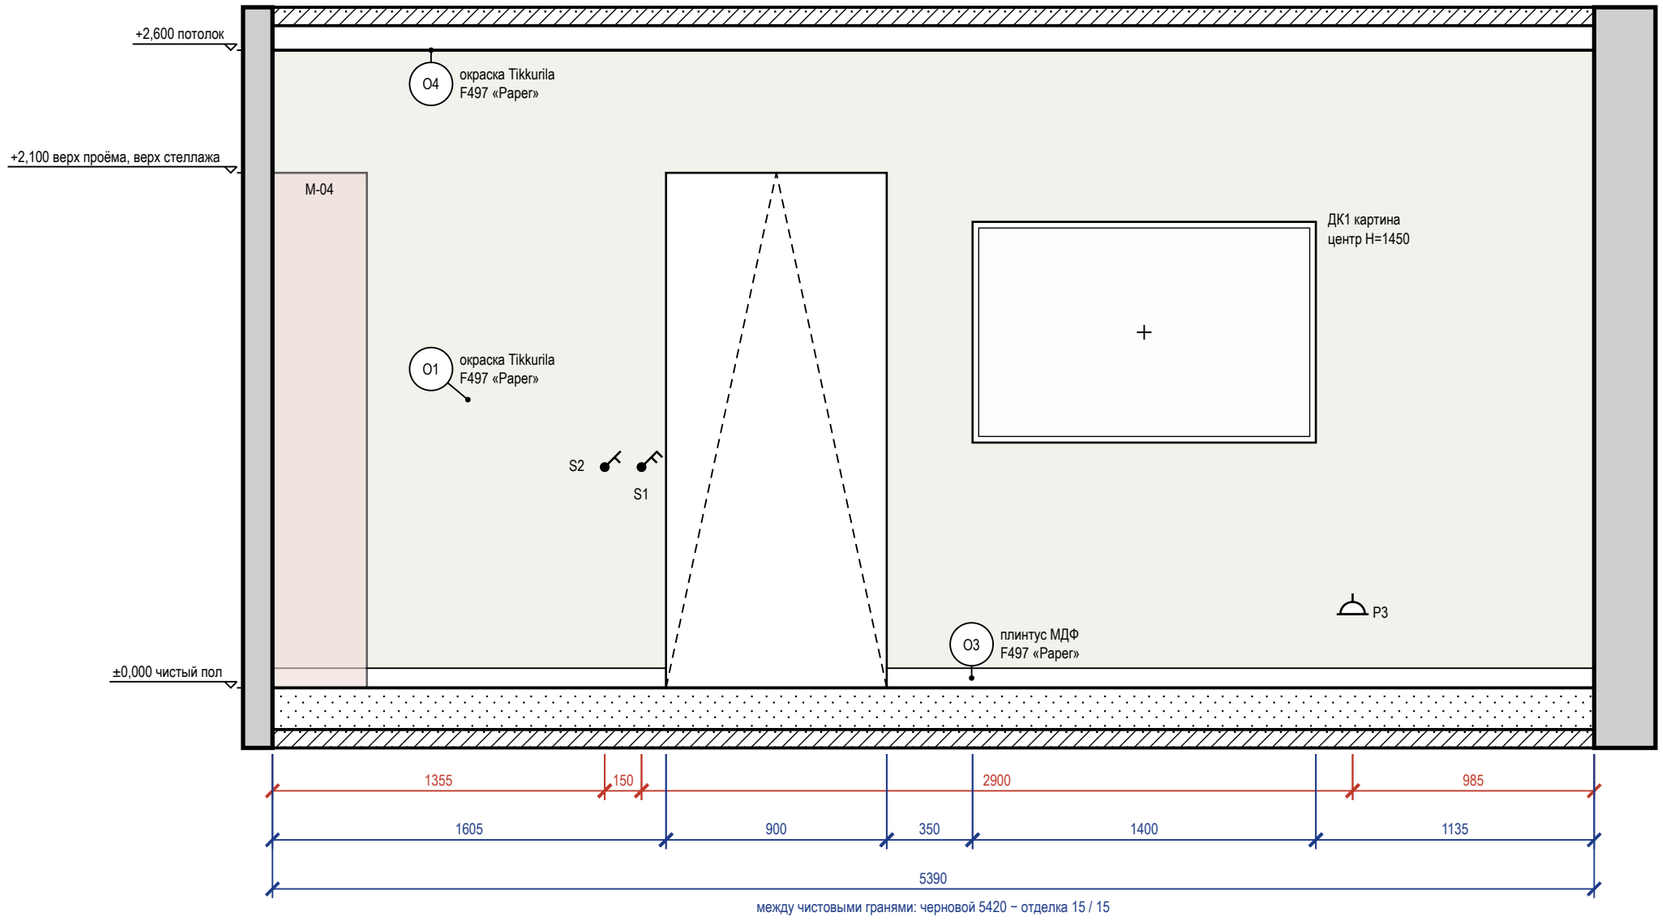


Схема развёрток (М 1:100)

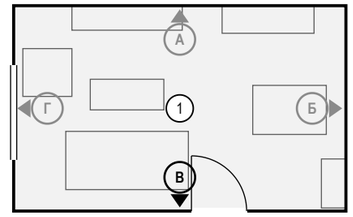


Ведомость точек и выводов

Марка	Что это	Гр.	H, мм	От угла, мм	Примечание
S2	выключатель	1	900	1355	
S1	выключатель	1	900	1505	
Р3	розетка: торшер у дивана М-01	5	300	4405	

Ведомость изделий и проёмов (на листе)

Марка	Изделие, проём	На виде Ш×В, мм	Низ, мм
М-04	стеллаж-витрина	385×2100	0
ДК1	картина	1400×900	1000

Стена В — визуализация, лист 5

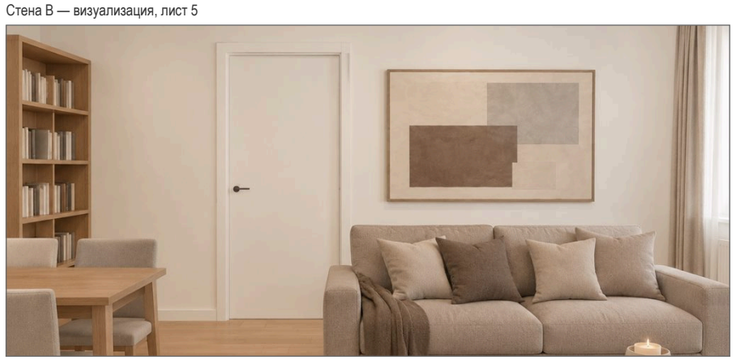

Ведомость отделки (на листе)


Марка	Поверхность	Материал, изделие	Цвет, код	Кол.
О1	стены	окраска, Tikkurila Optiva 5 Matt, матовая, подготовка К3	Tikkurila F497 «Paper»	12,1 м²
О3	плинтус	плинтус МДФ, h 80 мм, аналог: плинтус МДФ под окраску 80×16 мм, полуглянцевая	Tikkurila F497 «Paper»	4,5 м
О4	потолок	окраска, Tikkurila Anti-Reflex 2, глубокоматовая, подготовка Q3	Tikkurila F497 «Paper»	18,2 м²

Примечания

1. Размеры — в мм от чистовых поверхностей стен; условные обозначения и общие указания — лист 19.
2. Картины и зеркала крепить к основанию по паспорту изделия (закладные и анкеры — в перечне скрытых работ); крест — ось центра предмета.
3. Потолок — у каждой стены свой, по плану потолков (ПТ2); ступени — зоной, кромка короба перед нишей — тонкой линией; в поле потолка: ПТ1 +2,500.

	Лист	№ док.	Подпись	Дата	Проект: Четырёхкомнатная квартира	М 1:25
Дизайнер	Кырлан А.С.			14.11.26		
Проверил					Развёртка стены В. Зал (пом. 1)	Стадия: П; Лист: 72; Листов: 147
Н. контр.						
Утв.						

Стена Г (М 1:20)

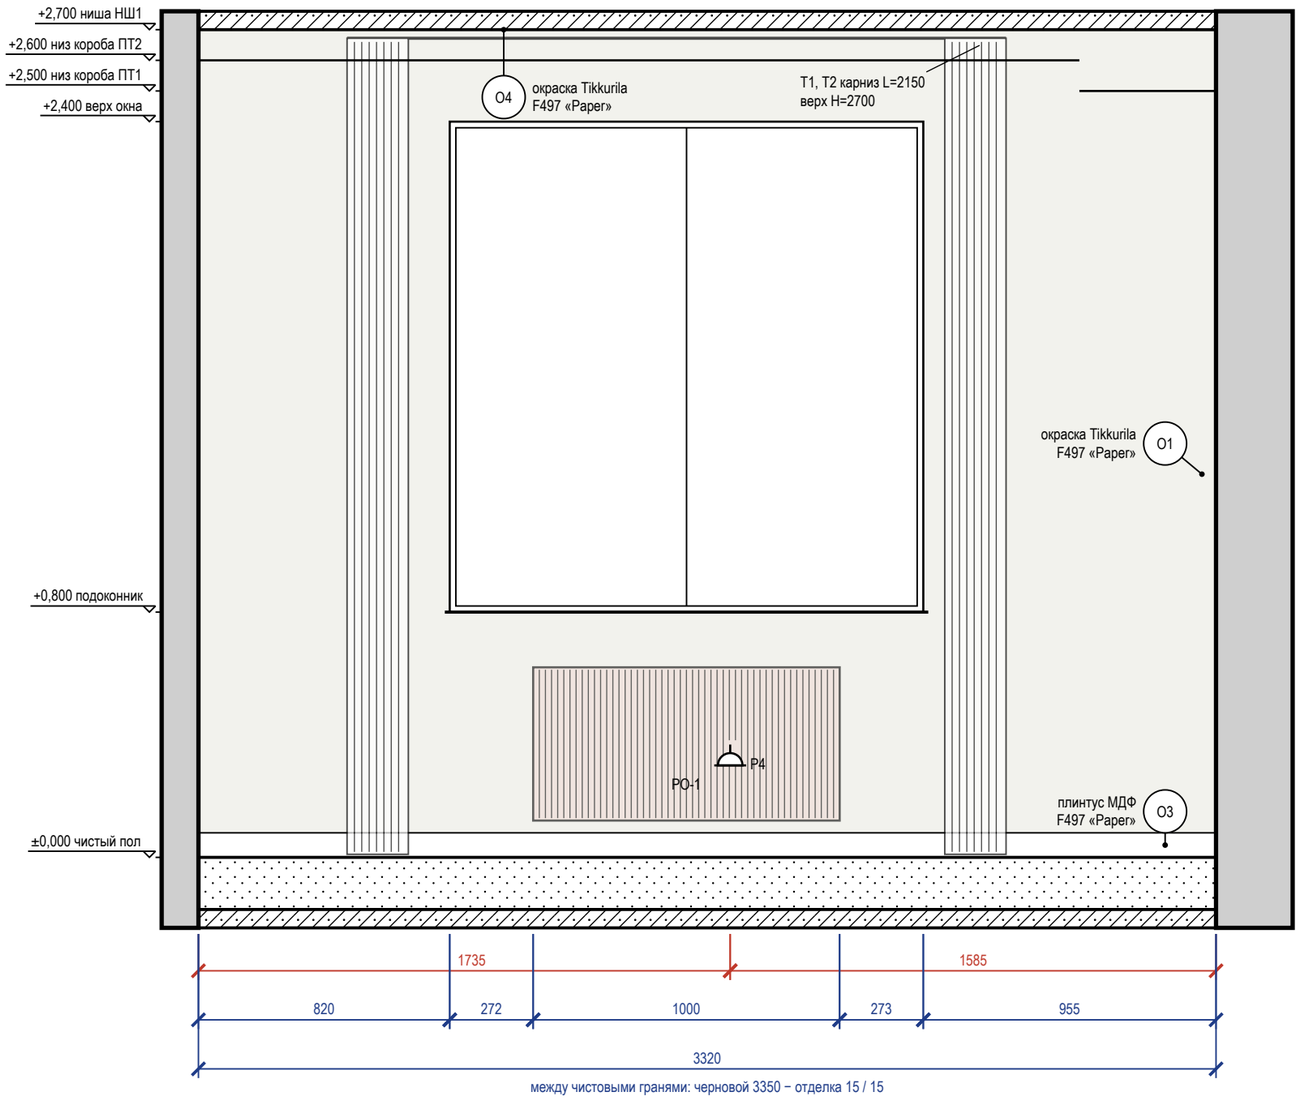

Ведомость точек и выводов

Марка	Что это	Гр.	H, мм	От угла, мм	Примечание
Р4	розетка: кресло у окна М-03	5	300	1735	

Ведомость изделий и проёмов (на листе)

Марка	Изделие, проём	На виде Ш×В, мм	Низ, мм
РО-1	радиатор отопления	1000×500	120

Примечания

1. Размеры — в мм от чистовых поверхностей стен; условные обозначения и общие указания — лист 19.
2. Карнизы (шины) — по ведомости текстиля декоратора: длина L и верх H на развёртке — те же числа, что в ведомости; крепление — до окраски потолка.
3. Потолок — у каждой стены свой, по плану потолков (НШ1, ПТ2, ПТ1); ступени — зоной, кромка короба перед нишей — тонкой линией.
4. Линии узора (швы плитки, складки штор, рёбра радиаторов) прерываются у знаков и выносок — просвет между линиями не менее 0,7 мм.


Стена Г — визуализация, лист 6



Ведомость отделки (на листе)

Марка	Поверхность	Материал, изделие	Цвет, код	Кол.
О1	стены	окраска, Tikkurila Optiva 5 Matt, матовая, подготовка К3	Tikkurila F497 «Paper»	6,5 м²
О3	плинтус	плинтус МДФ, h 80 мм, аналог: плинтус МДФ под окраску 80×16 мм, полуглянцевая	Tikkurila F497 «Paper»	3,3 м
О4	потолок	окраска, Tikkurila Anti-Reflex 2, глубокоматовая, подготовка Q3	Tikkurila F497 «Paper»	18,2 м²

Схема развёрток (М 1:50)

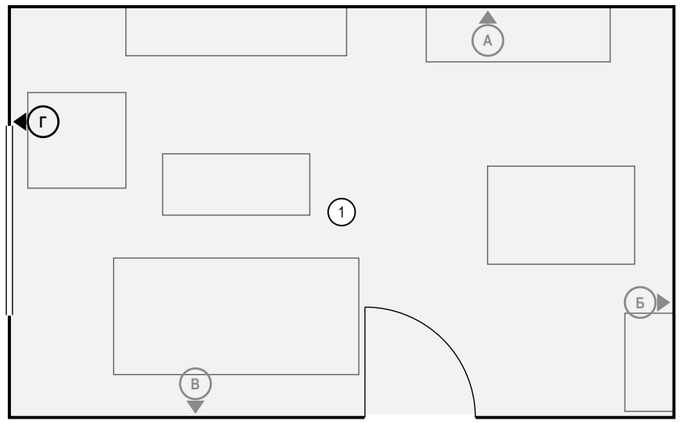

	Лист	№ док.	Подпись	Дата
Дизайнер	Кырлан А.С.			14.11.26
Проверил				
Н. контр.				
Утв.				

Проект: Четырёхкомнатная квартира — М 1:20

Развёртка стены Г. Зал (пом. 1)

Стадия	Лист	Листов
П	73	147

выпуск 14.11.2026 № e7147312ff · стр. 73 из 147

Стена А (М 1:20)


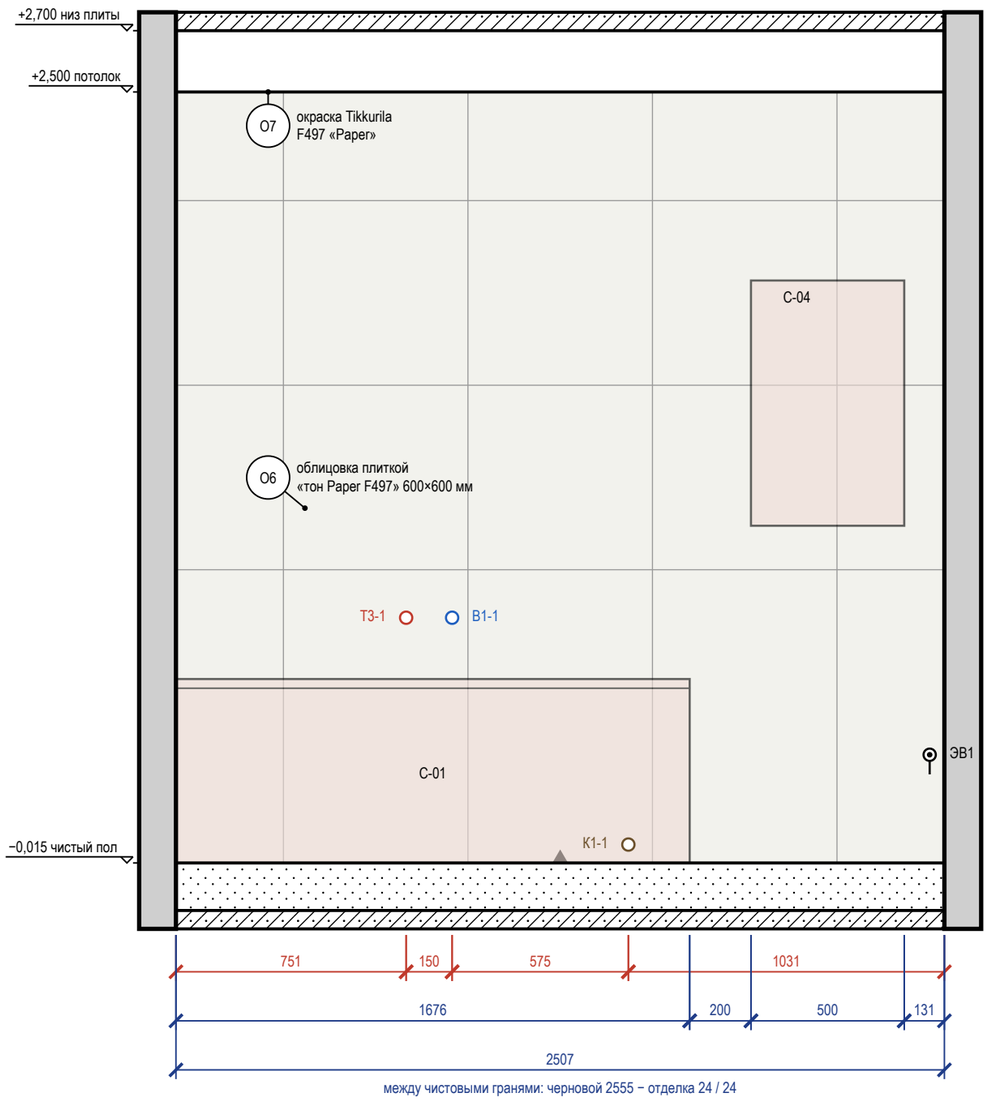


Схема развёрток (М 1:50)

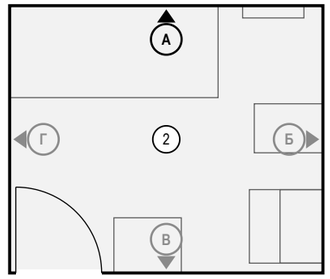

Ведомость точек и выводов

Марка	Что это	Гр.	Н, мм	От угла, мм	Примечание
Т3-1	горячая вода — ванна		800	751	межос. 150
В1-1	холодная вода — ванна		800	901	межос. 150
К1-1	канализация — ванна		60	1476	Ø50
ЭВ1	вывод кабеля: полотенцесушитель электрический С-04	16	353	2459	

Ведомость отделки (на листе)

Марка	Поверхность	Материал, изделие	Цвет, код	Кол.
О6	стены	облицовка плиткой, 600×600×9 мм, аналог: керамогранит матовый, тон F497, затирка CG2WA	#F1F1EC «тон Paper F497»	6,3 м²
О7	потолок	окраска, Tikkurila Luja 7, матовая, подготовка Q3	Tikkurila F497 «Paper»	5,6 м²

Ведомость изделий и проёмов (на листе)

Марка	Изделие, проём	На виде Ш×В, мм	Низ, мм
С-01	ванна акриловая 1700×750	1676×600	0
С-04	полотенцесушитель электрический, 500×800, IP44	500×800	1100

Примечания

1. Размеры — в мм от чистовых поверхностей стен; условные обозначения и общие указания — лист 19.
2. Облицовка — по сетке швов 2 мм, раскладка от оси стены (треугольник у пола), по высоте — от середины облицовки, подрезки у пола и у потолка поровну; подрезки — по листу раскладки плитки.
3. Гидроизоляция в 2 слоя, заход на стены 200 мм; над ванной — до 2100 и 300 мм за борт — до облицовки, с актом скрытых работ и тестом проливом (узел — на листе узлов).

	Лист	№ док.	Подпись	Дата
Дизайнер	Кырлан А.С.			14.11.26
Проверил				
Н. контр.				
Утв.				


Проект: Четырёхкомнатная квартира — **М 1:20**

Развёртка стены А. Ванная комната (пом. 2)

Стадия	Лист	Листов
П	74	147

выпуск 14.11.2026 № e7147312ff · стр. 74 из 147


Стена Б (М 1:20)

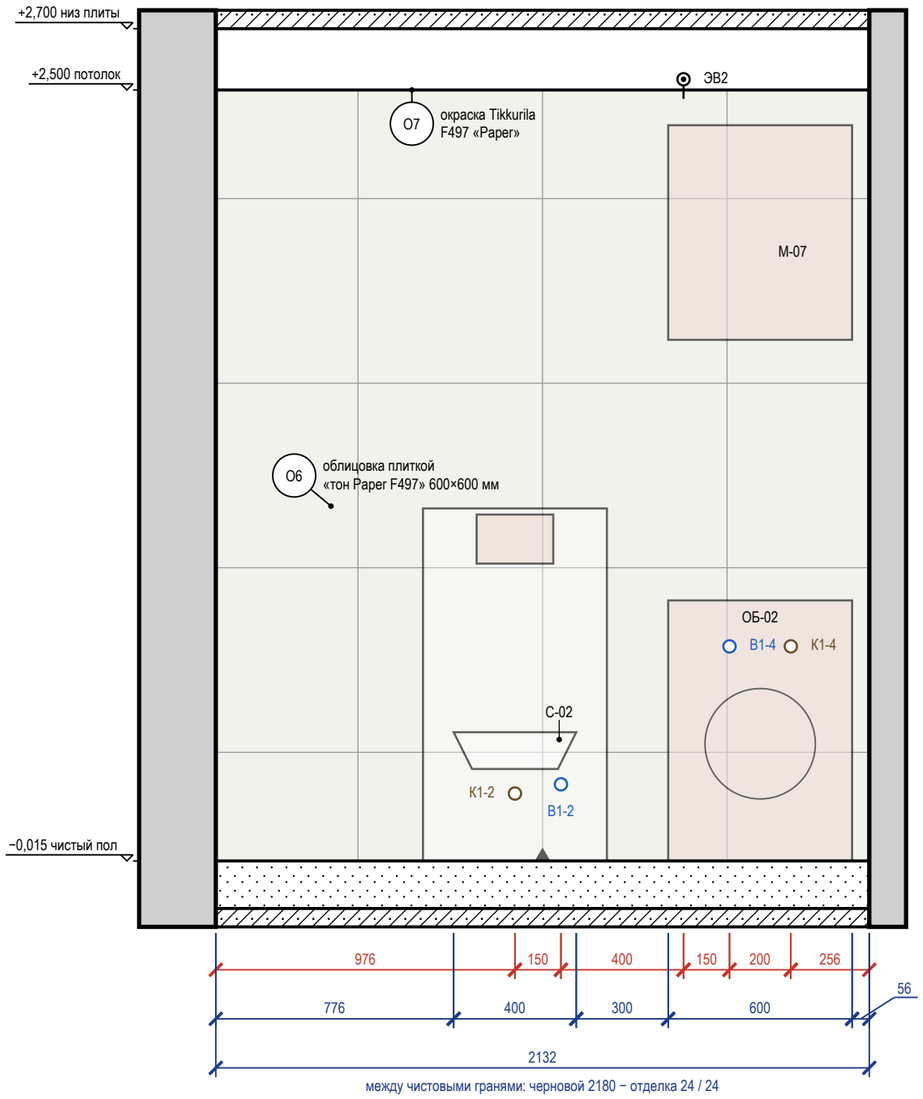

Стена Б — визуализация, лист 7



Схема развёрток (М 1:50)

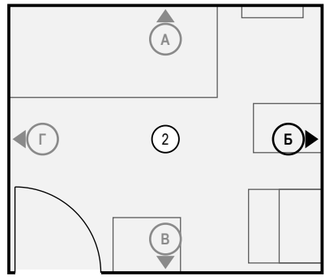

Ведомость точек и выводов

Марка	Что это	Гр.	Н, мм	От угла, мм	Примечание
К1-2	канализация — унитаз подвесной		220	976	Ø110
В1-2	холодная вода — унитаз подвесной		250	1126	в раме инсталляции
ЭВ2	вывод кабеля: вентилятор ВР1 (таймер выбега)	4	2550	1526	
В1-4	холодная вода — стиральная машина		700	1676	кран машины
К1-4	канализация — стиральная машина		700	1876	Ø40

Ведомость отделки (на листе)

Марка	Поверхность	Материал, изделие	Цвет, код	Кол.
О6	стены	облицовка плиткой, 600×600×9 мм, аналог: керамогранит матовый, тон F497, затирка CG2WA	#F1F1EC «тон Paper F497»	5,4 м²
О7	потолок	окраска, Tikkurila Luja 7, матовая, подготовка Q3	Tikkurila F497 «Paper»	5,6 м²

Ведомость изделий и проёмов (на листе)

Марка	Изделие, проём	На виде Ш×В, мм	Низ, мм
С-02	унитаз подвесной с инсталляцией	400×120	300
ОБ-02	стиральная машина 600×600, фронтальная загрузка	600×850	0
М-07	шкаф навесной над стиральной машиной	600×700	1700


Примечания

1. Размеры — в мм от чистовых поверхностей стен; условные обозначения и общие указания — лист 19.
2. Схема мебели, приборов и декора не является технической документацией для производства мебели; габариты — по паспортам изделий.
3. Облицовка — по сетке швов 2 мм, раскладка от оси стены (треугольник у пола), по высоте — от середины облицовки, подрезки у пола и у потолка поровну; подрезки — по листу раскладки плитки.
4. Гидроизоляция в 2 слоя, заход на стены 200 мм; над ванной — до 2100 и 300 мм за борт — до облицовки, с актом скрытых работ и тестом проливом (узел — на листе узлов).

	Лист	№ док.	Подпись	Дата	Проект: Четырёхкомнатная квартира	М 1:20	
Дизайнер	Кырлан А.С.			14.11.26			
Проверил					Развёртка стены Б. Ванная комната (пом. 2)	Стадия	Лист	Листов
Н. контр.						П	75	147
Утв.								


выпуск 14.11.2026 № e7147312ff · стр. 75 из 147

Стена В (М 1:20)

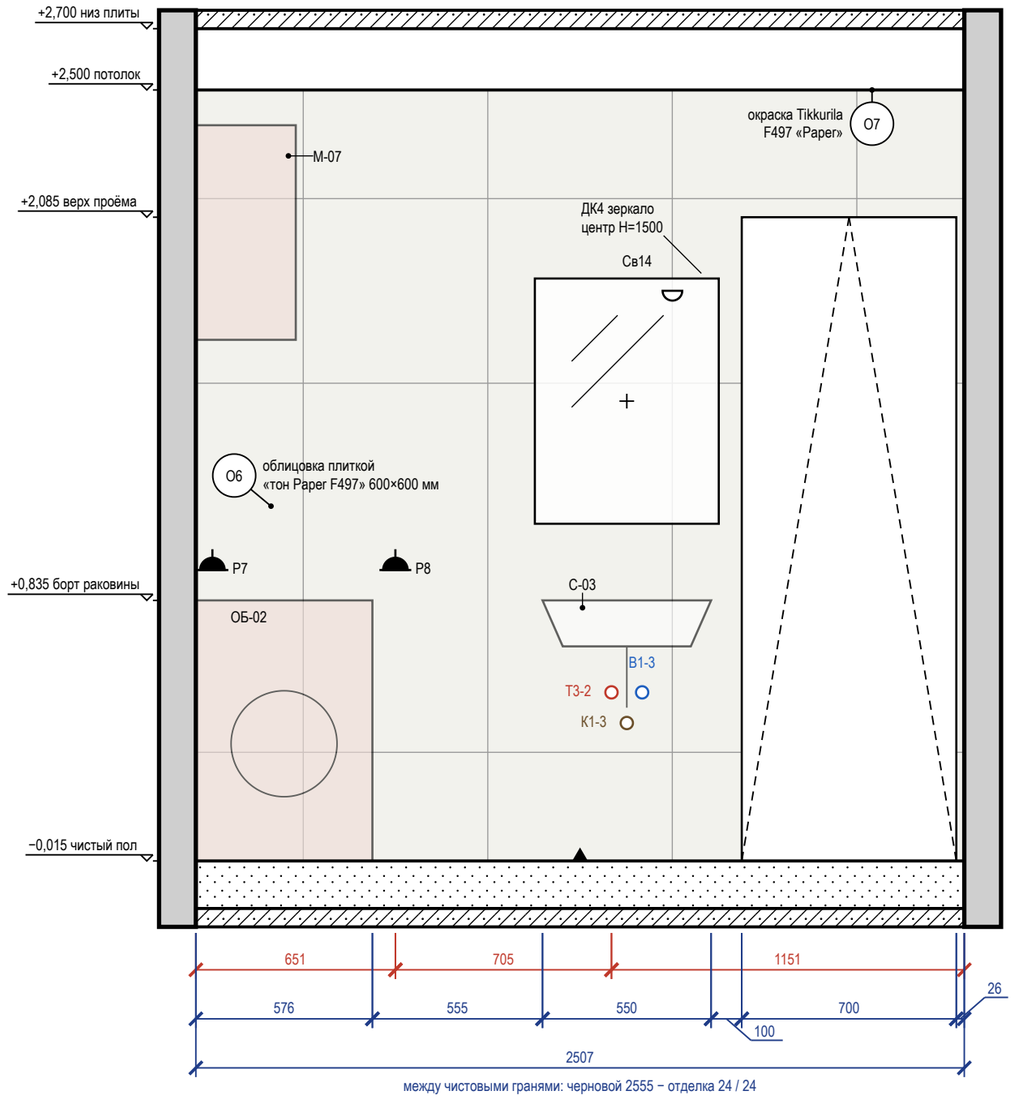


между чистовыми гранями: черновой 2555 − отделка 24 / 24

Стена Г (М 1:20)

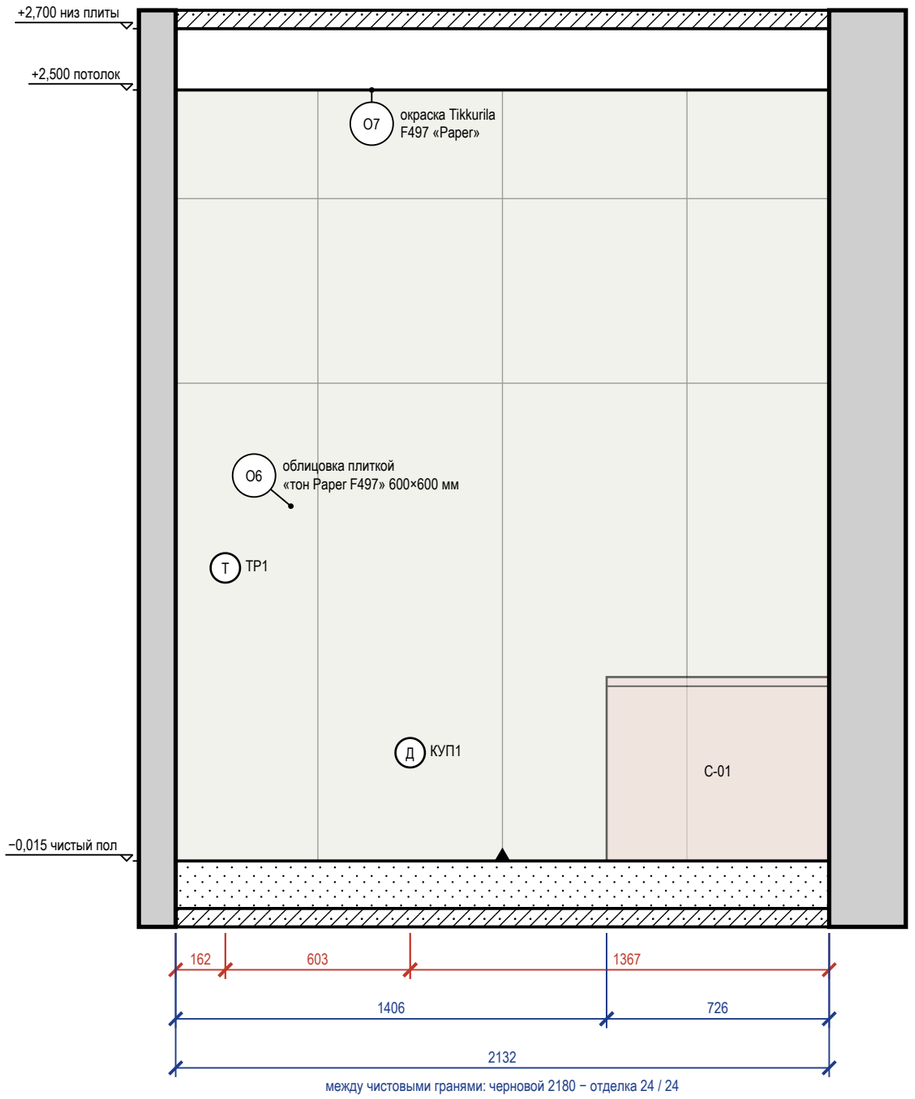

между чистовыми гранями: черновой 2180 − отделка 24 / 24

Схема развёрток (М 1:100)

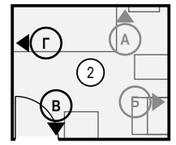

Ведомость точек и выводов

Стена	Марка	Что это	Гр.	Н, мм	От угла, мм	Примечание
В	Р7	розетка: стиральная машина	14	949	48	IP44
В	Р8	розетка: фен у умывальника	15	949	651	IP44
В	Т3-2	горячая вода — умывальник		550	1356	межос. 100
В	К1-3	канализация — умывальник		450	1406	Ø40

Стена	Марка	Что это	Гр.	Н, мм	От угла, мм	Примечание
В	В1-3	холодная вода — умывальник		550	1456	межос. 100
В	Св14	светильник настенный	4	1860	1555	
Г	ТР1	терморегулятор: терморегулятор тёплого пола ванной	17	956	162	
Г	КУП1	КУП (уравнивание потенциалов): КУП коробка уравнивания потенциалов (ДСУП)		353	765	

Ведомость отделки (на листе)

Марка	Поверхность	Материал, изделие	Цвет, код	Кол.
О6	стены	облицовка плиткой, 600×600×9 мм, аналог: керамогранит матовый, тон F497, затирка CG2WA	#F1F1EC «тон Paper F497»	10,2 м²
О7	потолок	окраска, Tikkurila Luja 7, матовая, подготовка Q3	Tikkurila F497 «Paper»	5,6 м²

Примечания

1. Размеры — в мм от чистовых поверхностей стен; условные обозначения и общие указания — лист 19.
2. Схема мебели, приборов и декора не является технической документацией для производства мебели; габариты — по паспортам изделий.
3. Облицовка — по сетке швов 2 мм, раскладка от оси стены (треугольник у пола), по высоте — от середины облицовки, подрезки у пола и у потолка поровну; подрезки — по листу раскладки плитки.
4. Гидроизоляция в 2 слоя, заход на стены 200 мм; над ванной — до 2100 и 300 мм за борт — до облицовки, с актом скрытых работ и тестом проливом (узел — на листе узлов).
5. Картины и зеркала крепить к основанию по паспорту изделия (закладные и анкеры — в перечне скрытых работ); крест — ось центра предмета.

	Лист	№ док.	Подпись	Дата
Дизайнер	Кырлан А.С.			14.11.26
Проверил				
Н. контр.				
Утв.				


Проект: Четырёхкомнатная квартира — М 1:20

Развёртки стен В, Г. Ванная комната (пом. 2)


Стадия	Лист	Листов
П	76	147

выпуск 14.11.2026 № e7147312ff · стр. 76 из 147

Стена А (М 1:20)

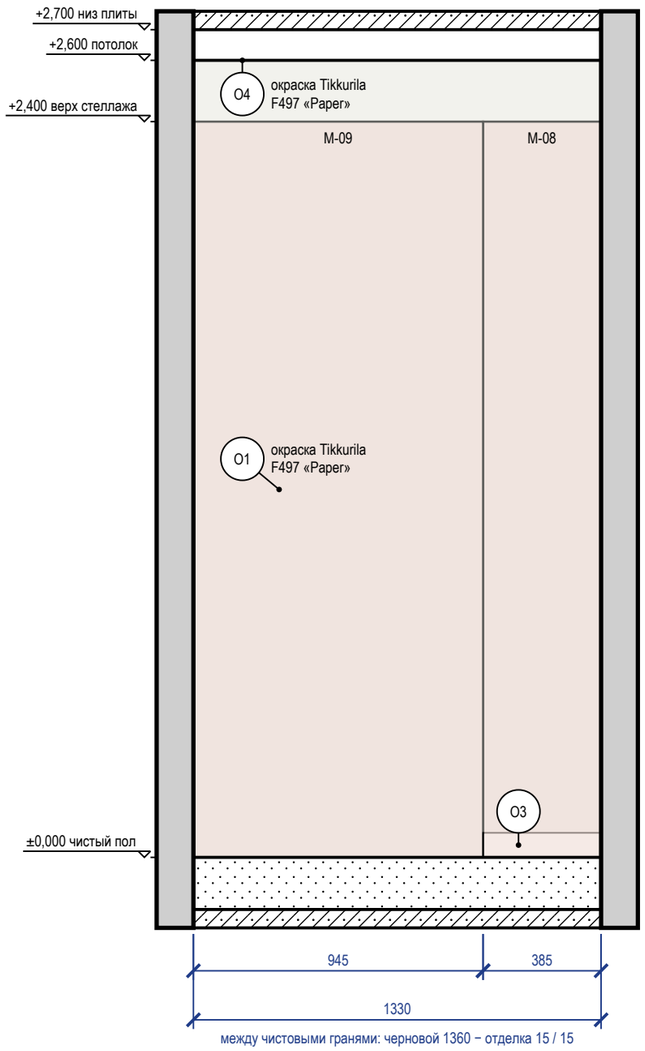

Стена Б (М 1:20)

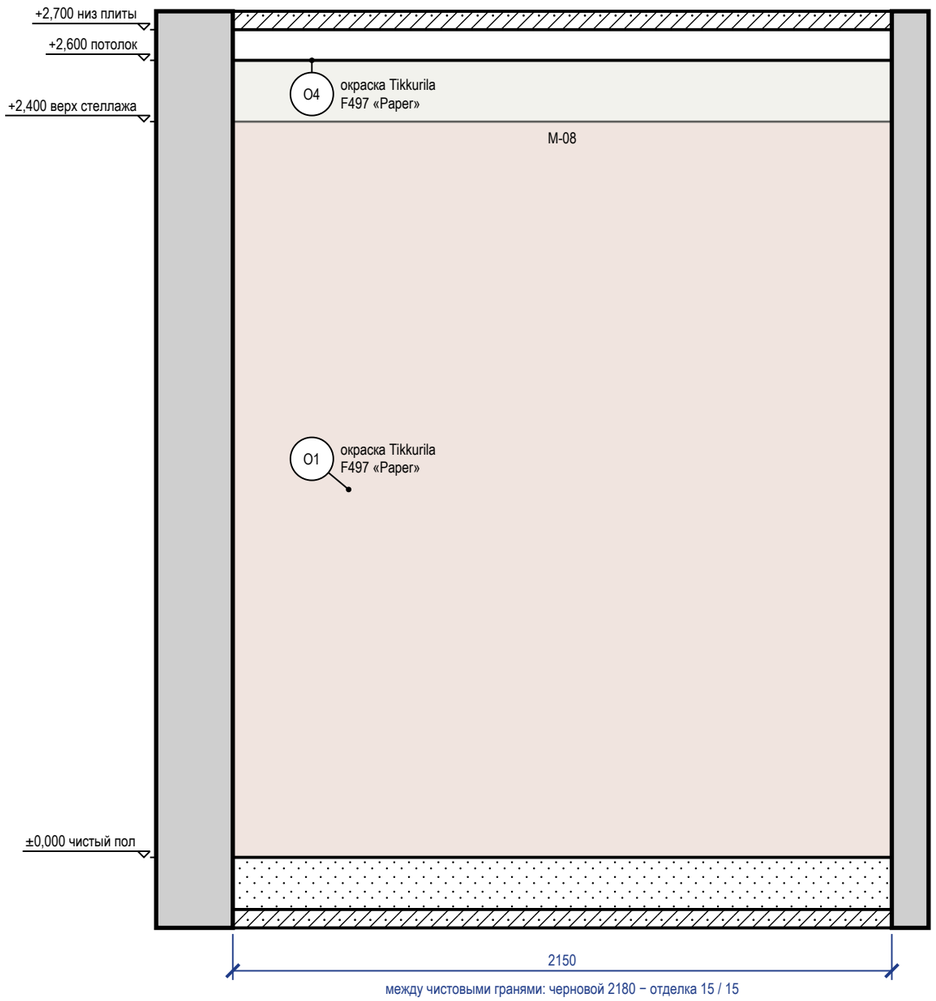

Ведомость изделий и проёмов (на листе)

Стена	Марка	Изделие, проём	На виде Ш×В, мм	Низ, мм
А	М-09	стеллаж хозяйственный, 6 полок	945×2400	0
А	М-08	стеллаж хозяйственный, 6 полок	385×2400	0
Б	М-08	стеллаж хозяйственный, 6 полок	2150×2400	0


Стена А — визуализация, лист 8



Ведомость отделки (на листе)

Марка	Поверхность	Материал, изделие	Цвет, код	Кол.
О1	стены	окраска, Tikkurila Optiva 5 Matt, матовая, подготовка К3	Tikkurila F497 «Paper»	9 м²
О3	плинтус	плинтус МДФ, h 80 мм, аналог: плинтус МДФ под окраску 80×16 мм, полуглянцевая	Tikkurila F497 «Paper»	0,4 м
О4	потолок	окраска, Tikkurila Anti-Reflex 2, глубокоматовая, подготовка Q3	Tikkurila F497 «Paper»	3 м²

Схема развёрток (М 1:50)

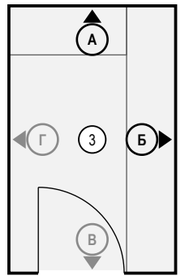


Примечания

1. Размеры — в мм от чистовых поверхностей стен; условные обозначения и общие указания — лист 19.

	Лист	№ док.	Подпись	Дата	Проект: Четырёхкомнатная квартира			М 1:20
Дизайнер	Кырлан А.С.			14.11.26	Развёртки стен А, Б. Тёмная комната (пом. 3)	Стадия	Лист	Листов
Проверил						П	77	147
Н. контр.								
Утв.								


выпуск 14.11.2026 № e7147312ff · стр. 77 из 147

Стена В (М 1:20)

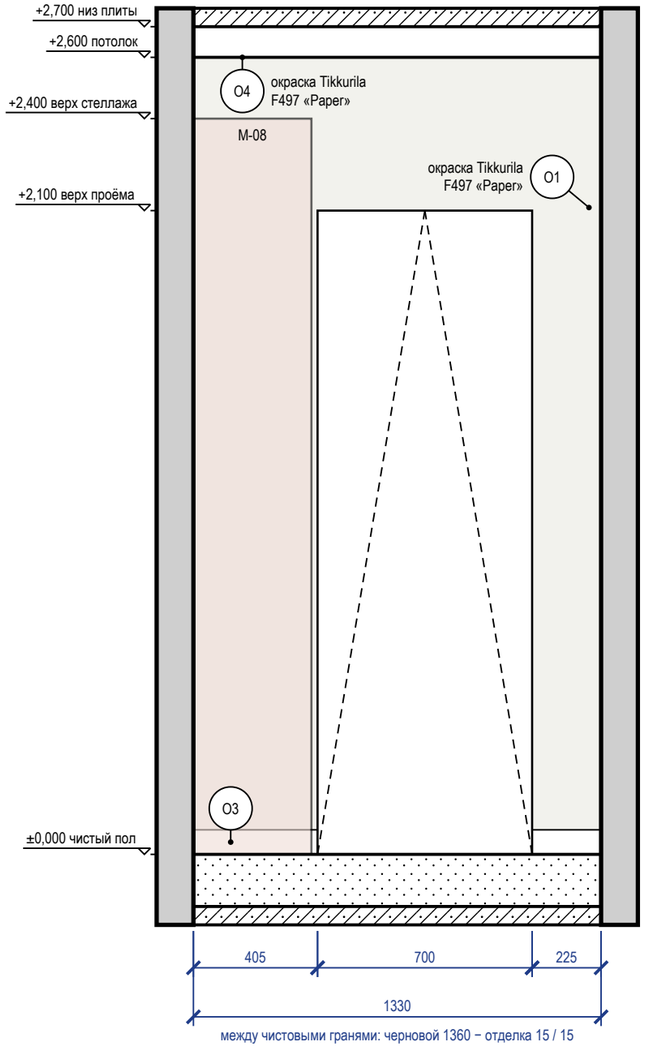

между чистовыми гранями: черновой 1360 − отделка 15 / 15

Стена Г (М 1:20)

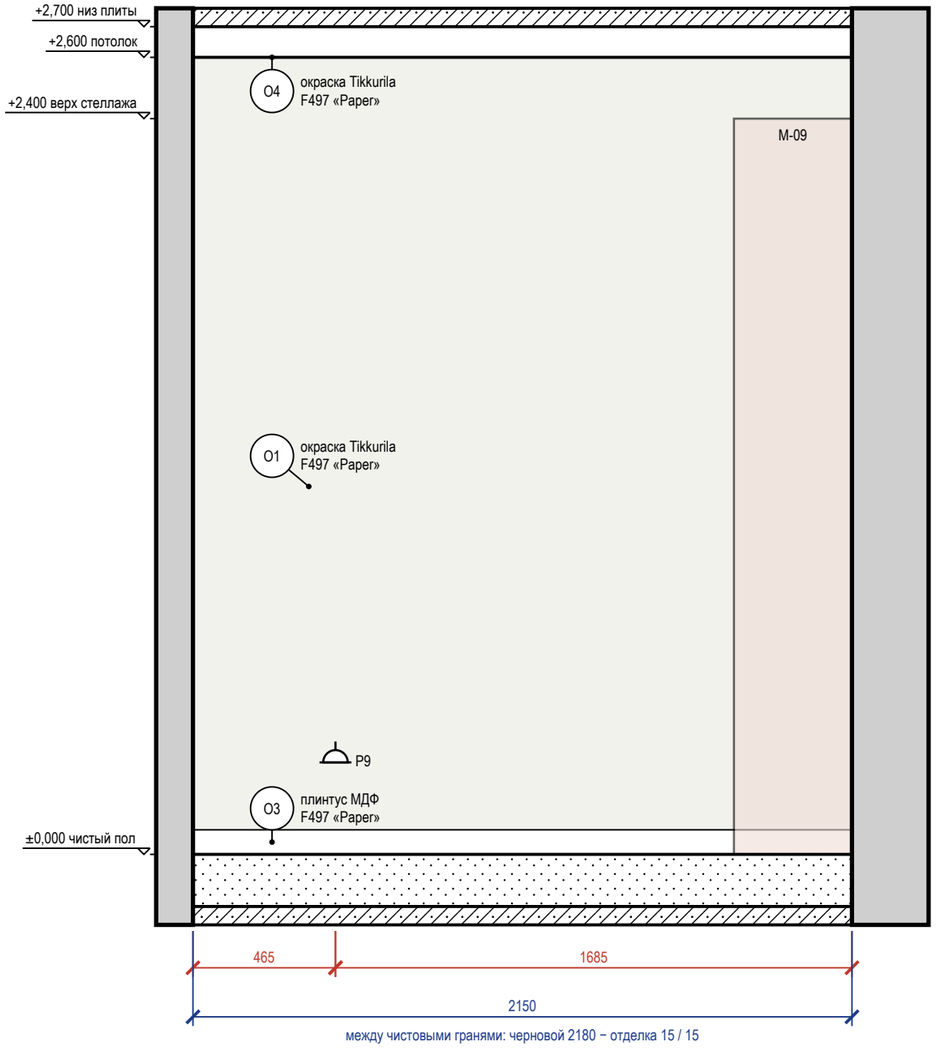

между чистовыми гранями: черновой 2180 − отделка 15 / 15

Ведомость точек и выводов

Стена	Марка	Что это	Гр.	Н, мм	От угла, мм	Примечание
Г	Р9	розетка: уборка, пылесос	8	300	465	


Ведомость изделий и проёмов (на листе)

Стена	Марка	Изделие, проём	На виде Ш×В, мм	Низ, мм
В	М-08	стеллаж хозяйственный, 6 полок	385×2400	0
Г	М-09	стеллаж хозяйственный, 6 полок	385×2400	0

Ведомость отделки (на листе)

Марка	Поверхность	Материал, изделие	Цвет, код	Кол.
О1	стены	окраска, Tikkurila Optiva 5 Matt, матовая, подготовка К3	Tikkurila F497 «Paper»	7,6 м²
О3	плинтус	плинтус МДФ, h 80 мм, аналог: плинтус МДФ под окраску 80×16 мм, полуглянцевая	Tikkurila F497 «Paper»	2,8 м
О4	потолок	окраска, Tikkurila Anti-Reflex 2, глубокоматовая, подготовка Q3	Tikkurila F497 «Paper»	3 м²

Схема развёрток (М 1:50)

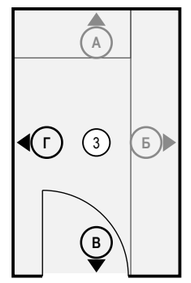


Примечания

1. Размеры — в мм от чистовых поверхностей стен; условные обозначения и общие указания — лист 19.

	Лист	№ док.	Подпись	Дата	Проект: Четырёхкомнатная квартира	М 1:20		
Дизайнер	Кырлан А.С.			14.11.26	Развёртки стен В, Г. Тёмная комната (пом. 3)	Стадия	Лист	Листов
Проверил						П	78	147
Н. контр.								
Утв.								

выпуск 14.11.2026 № e7147312ff · стр. 78 из 147

Стена А (М 1:20)

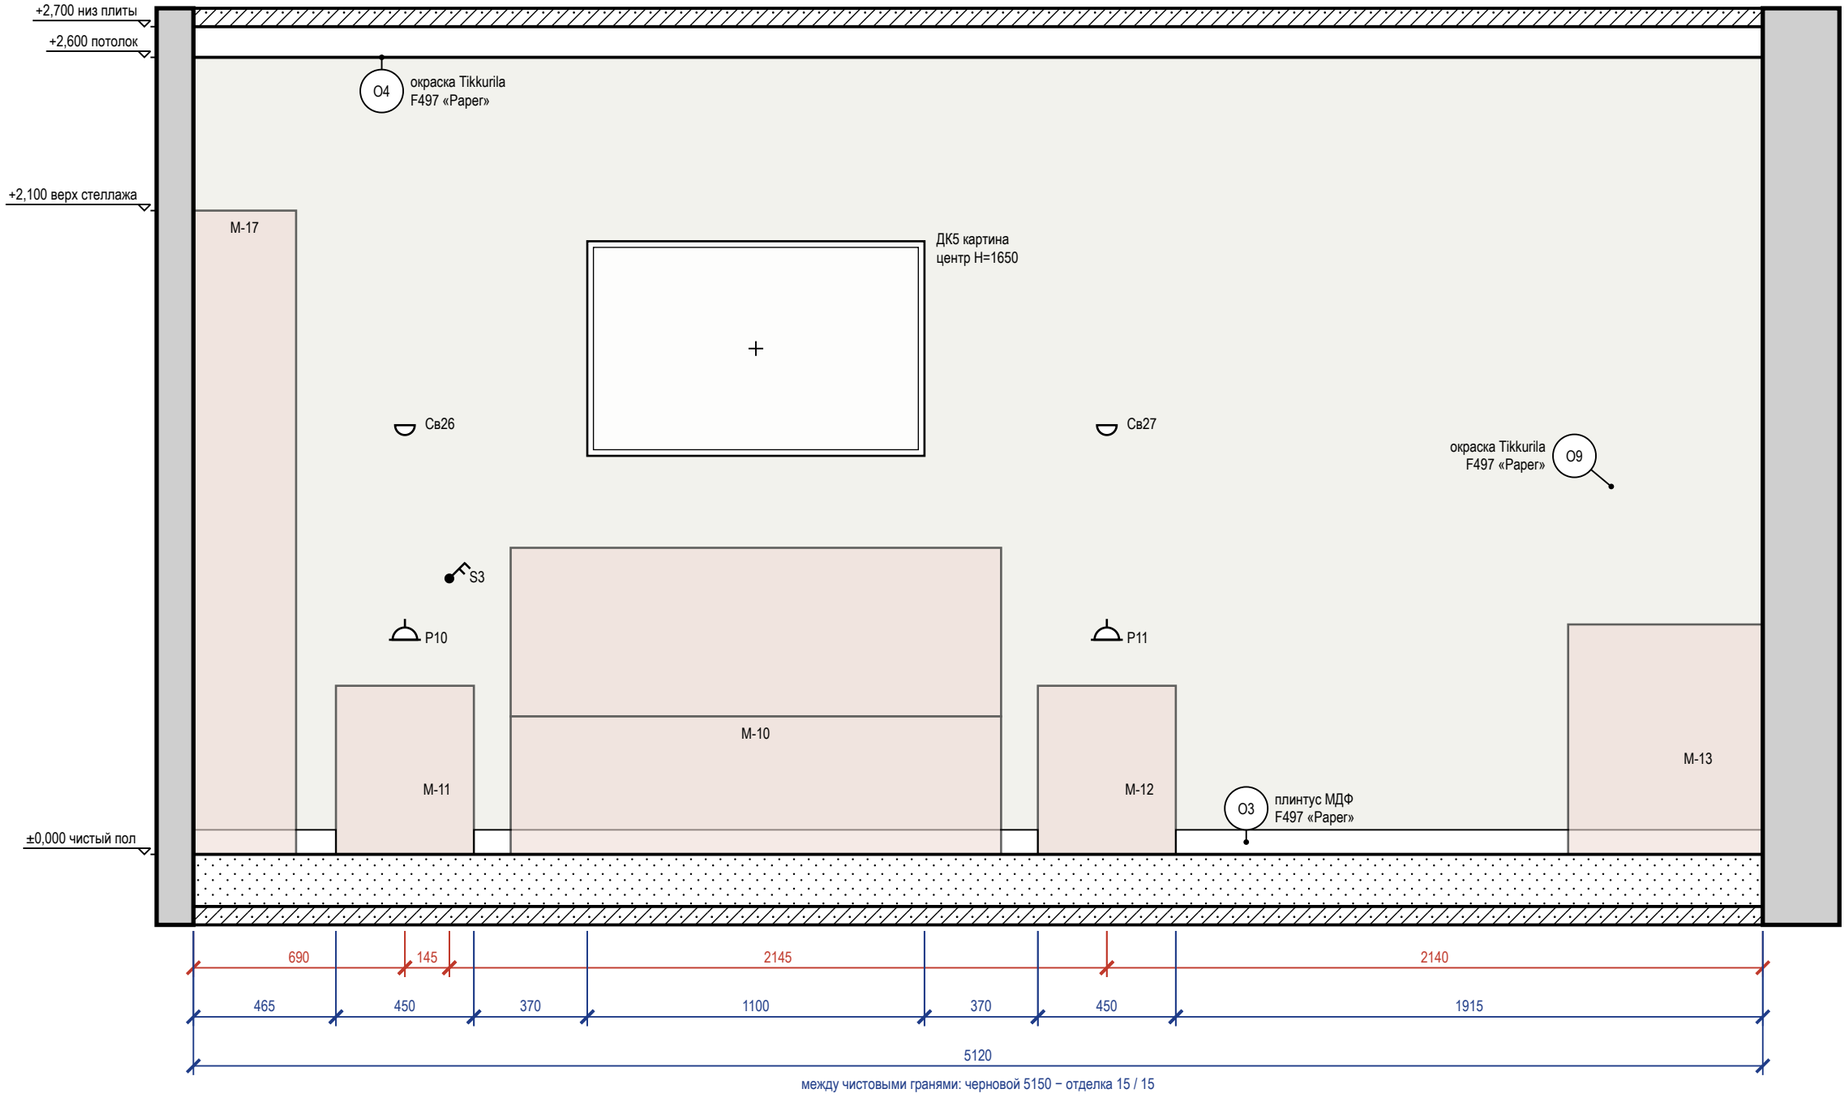


Ведомость точек и выводов

Марка	Что это	Гр.	Н, мм	От угла, мм	Примечание
Р10	розетка: у кровати, тумба М-11	6	700	690	
Св26	светильник настенный	3	1400	690	
S3	выключатель	3	900	835	
Р11	розетка: у кровати, тумба М-12	6	700	2980	
Св27	светильник настенный	3	1400	2980	

Ведомость отделки (на листе)

Марка	Поверхность	Материал, изделие	Цвет, код	Кол.
О3	плинтус	плинтус МДФ, h 80 мм, аналог: плинтус МДФ под окраску 80×16 мм, полуглянцевая	Tikkurila F497 «Paper»	4,2 м
О4	потолок	окраска, Tikkurila Anti-Reflex 2, глубокоматовая, подготовка Q3	Tikkurila F497 «Paper»	17,5 м²
О9	стены	окраска, Tikkurila Joker, шелковисто-матовая, подготовка К3	Tikkurila F497 «Paper»	13,3 м²

Схема развёрток (М 1:100)

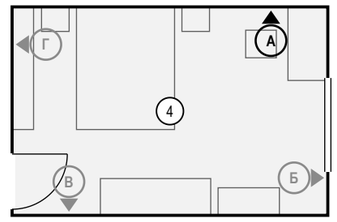


Примечания

1. Размеры — в мм от чистовых поверхностей стен; условные обозначения и общие указания — лист 19.
2. Картины и зеркала крепить к основанию по паспорту изделия (закладные и анкеры — в перечне скрытых работ); крест — ось центра предмета.

	Лист	№ док.	Подпись	Дата	Проект: Четырёхкомнатная квартира	М 1:20		
Дизайнер	Кырлан А.С.			14.11.26				
Проверил					Развёртка стены А. Детская 1 (пом. 4)	Стадия	Лист	Листов
Н. контр.						П	79	147
Утв.								


Стена Б (М 1:20)

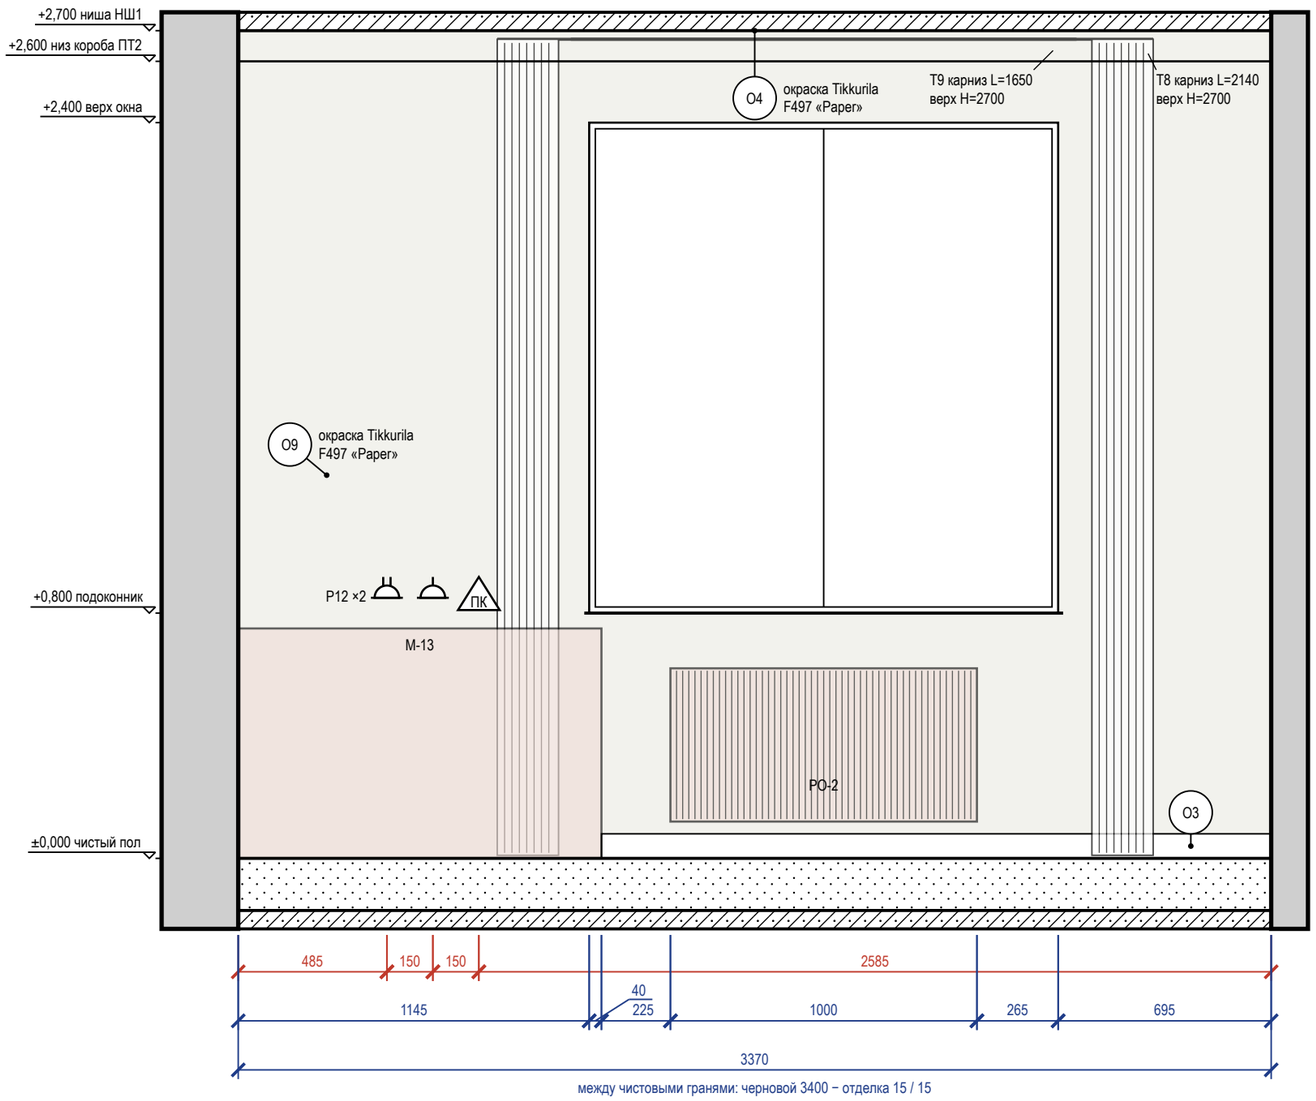

Ведомость отделки (на листе)

Марка	Поверхность	Материал, изделие	Цвет, код	Кол.
О3	плинтус	плинтус МДФ, h 80 мм, аналог: плинтус МДФ под окраску 80×16 мм, полуглянцевая	Tikkurila F497 «Paper»	2,2 м
О4	потолок	окраска, Tikkurila Anti-Reflex 2, глубокоматовая, подготовка Q3	Tikkurila F497 «Paper»	17,5 м²
О9	стены	окраска, Tikkurila Joker, шелковисто-матовая, подготовка К3	Tikkurila F497 «Paper»	6,7 м²

Схема развёрток (М 1:50)

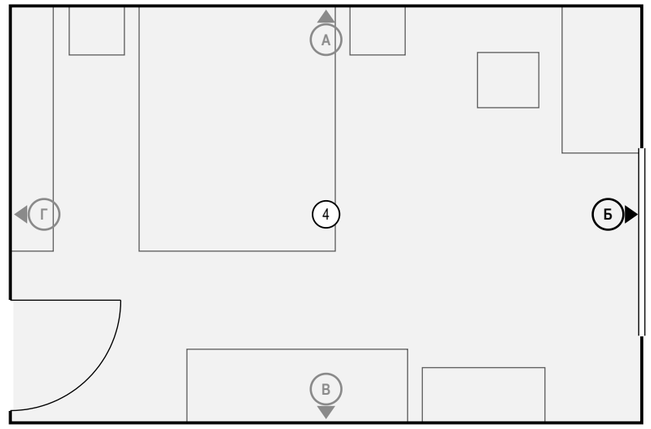

Ведомость точек и выводов

Марка	Что это	Гр.	Н, мм	От угла, мм	Примечание
Р12	розетка: рабочий стол М-13	6	850	485	рамка 2 поста
Р13	розетка: рабочий стол М-13	6	850	635	
LAN2	розетка RJ45: рабочий стол М-13		850	785	

Ведомость изделий и проёмов (на листе)

Марка	Изделие, проём	На виде Ш×В, мм	Низ, мм
М-13	стол письменный у окна	1185×750	0
РО-2	радиатор отопления	1000×500	120


Примечания

1. Размеры — в мм от чистовых поверхностей стен; условные обозначения и общие указания — лист 19.
2. Карнизы (шины) — по ведомости текстиля декоратора: длина L и верх H на развёртке — те же числа, что в ведомости; крепление — до окраски потолка.
3. Часть марок не уместилась у знаков: коды, высоты и привязки этих позиций — в ведомости точек и выводов под видами.

	Лист	№ док.	Подпись	Дата	Проект: Четырёхкомнатная квартира			М 1:20
Дизайнер	Кырлан А.С.			14.11.26				
Проверил					Развёртка стены Б. Детская 1 (пом. 4)	Стадия	Лист	Листов
Н. контр.						П	80	147
Утв.								

выпуск 14.11.2026 № e7147312ff · стр. 80 из 147

Стена В (М 1:25)

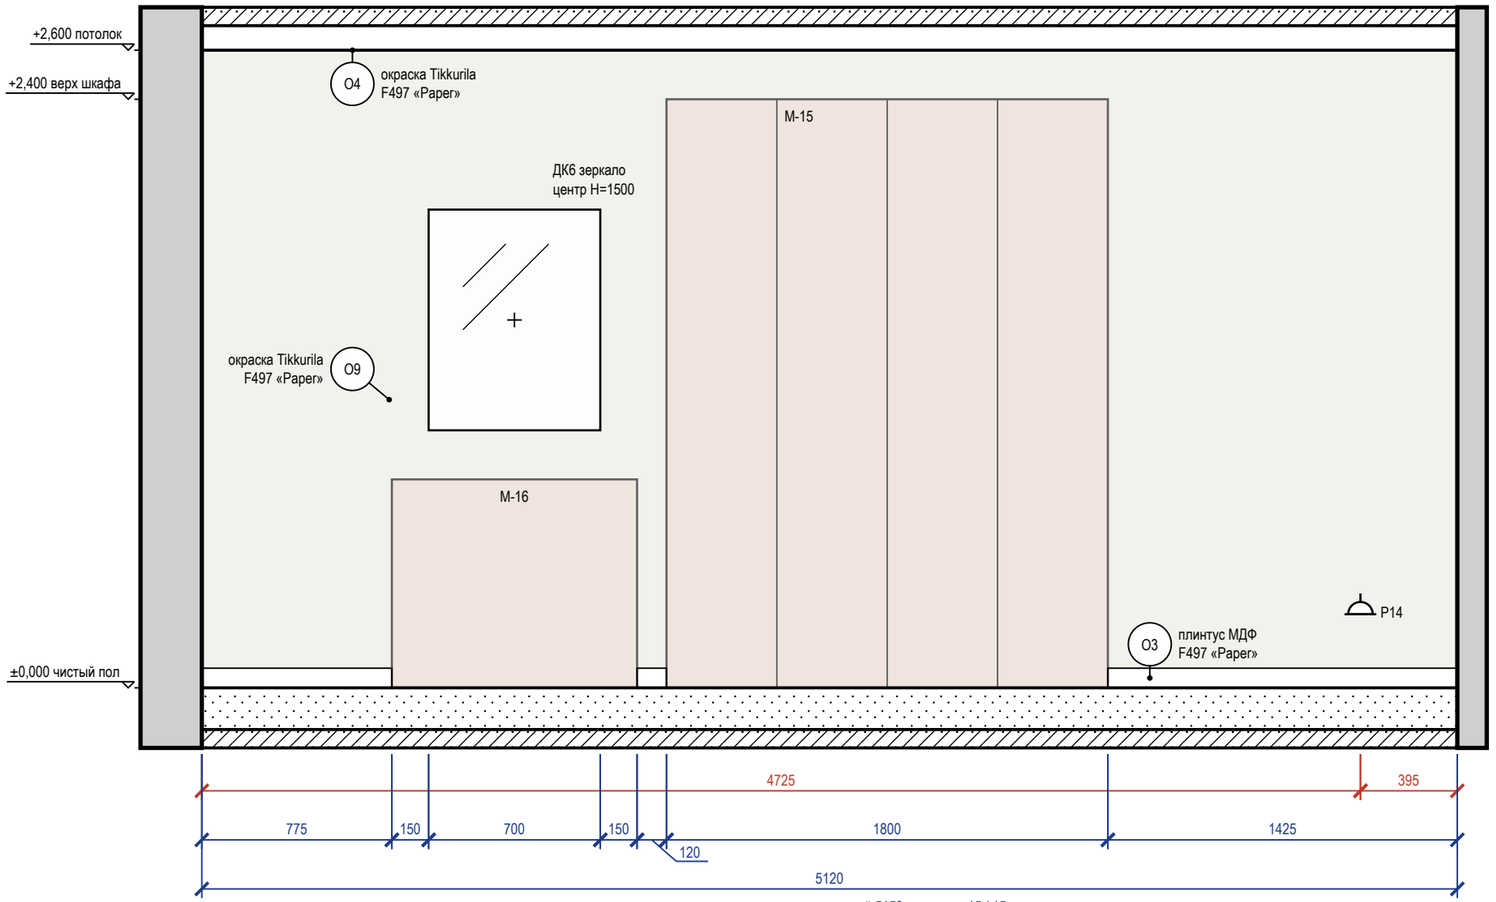

между чистовыми гранями: черновой 5150 − отделка 15 / 15

Стена В — визуализация, лист 9


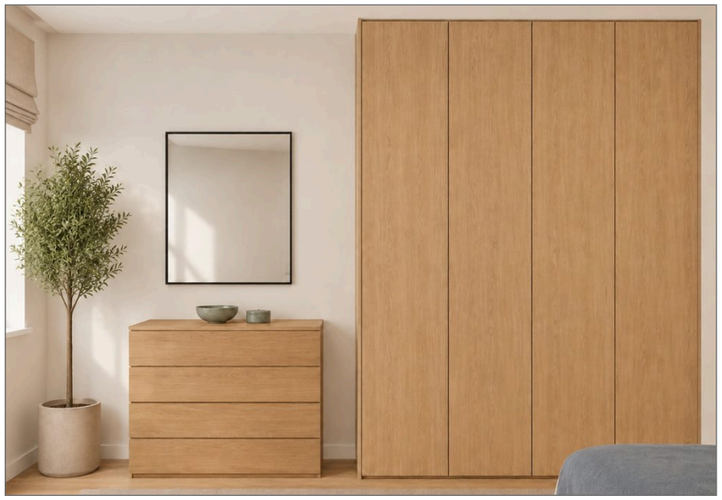


Схема развёрток (М 1:50)

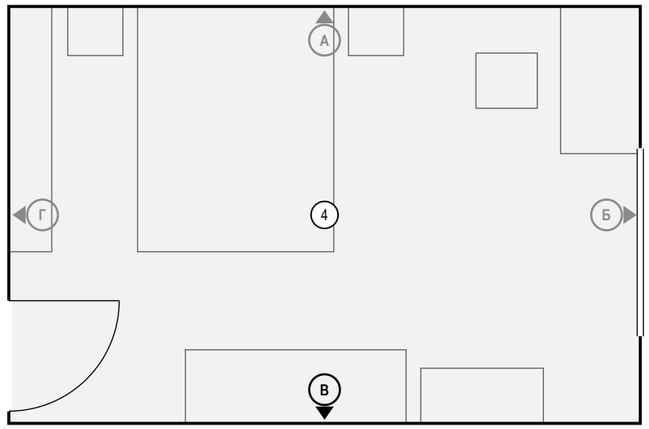

Ведомость точек и выводов

Марка	Что это	Гр.	H, мм	От угла, мм	Примечание
Р14	розетка: уборка	6	300	4725	

Ведомость изделий и проёмов (на листе)

Марка	Изделие, проём	На виде Ш×В, мм	Низ, мм
М-16	комод, 4 ящика	1000×850	0
ДК6	зеркало	700×900	1050
М-15	шкаф распашной, 4 створки	1800×2400	0

Ведомость отделки (на листе)

Марка	Поверхность	Материал, изделие	Цвет, код	Кол.
О3	плинтус	плинтус МДФ, h 80 мм, аналог: плинтус МДФ под окраску 80×16 мм, полуглянцевая	Tikkurila F497 «Paper»	2,3 м
О4	потолок	окраска, Tikkurila Anti-Reflex 2, глубокоматовая, подготовка Q3	Tikkurila F497 «Paper»	17,5 м²
О9	стены	окраска, Tikkurila Joker, шелковисто-матовая, подготовка К3	Tikkurila F497 «Paper»	13,3 м²

Примечания

1. Размеры — в мм от чистовых поверхностей стен; условные обозначения и общие указания — лист 19.
2. Картины и зеркала крепить к основанию по паспорту изделия (закладные и анкеры — в перечне скрытых работ); крест — ось центра предмета.

	Лист	№ док.	Подпись	Дата
Дизайнер	Кырлан А.С.			14.11.26
Проверил				
Н. контр.				
Утв.				


Проект: Четырёхкомнатная квартира — М 1:25

Развёртка стены В. Детская 1 (пом. 4)


Стадия	Лист	Листов
П	81	147

выпуск 14.11.2026 № e7147312ff · стр. 81 из 147

Стена Г (М 1:20)

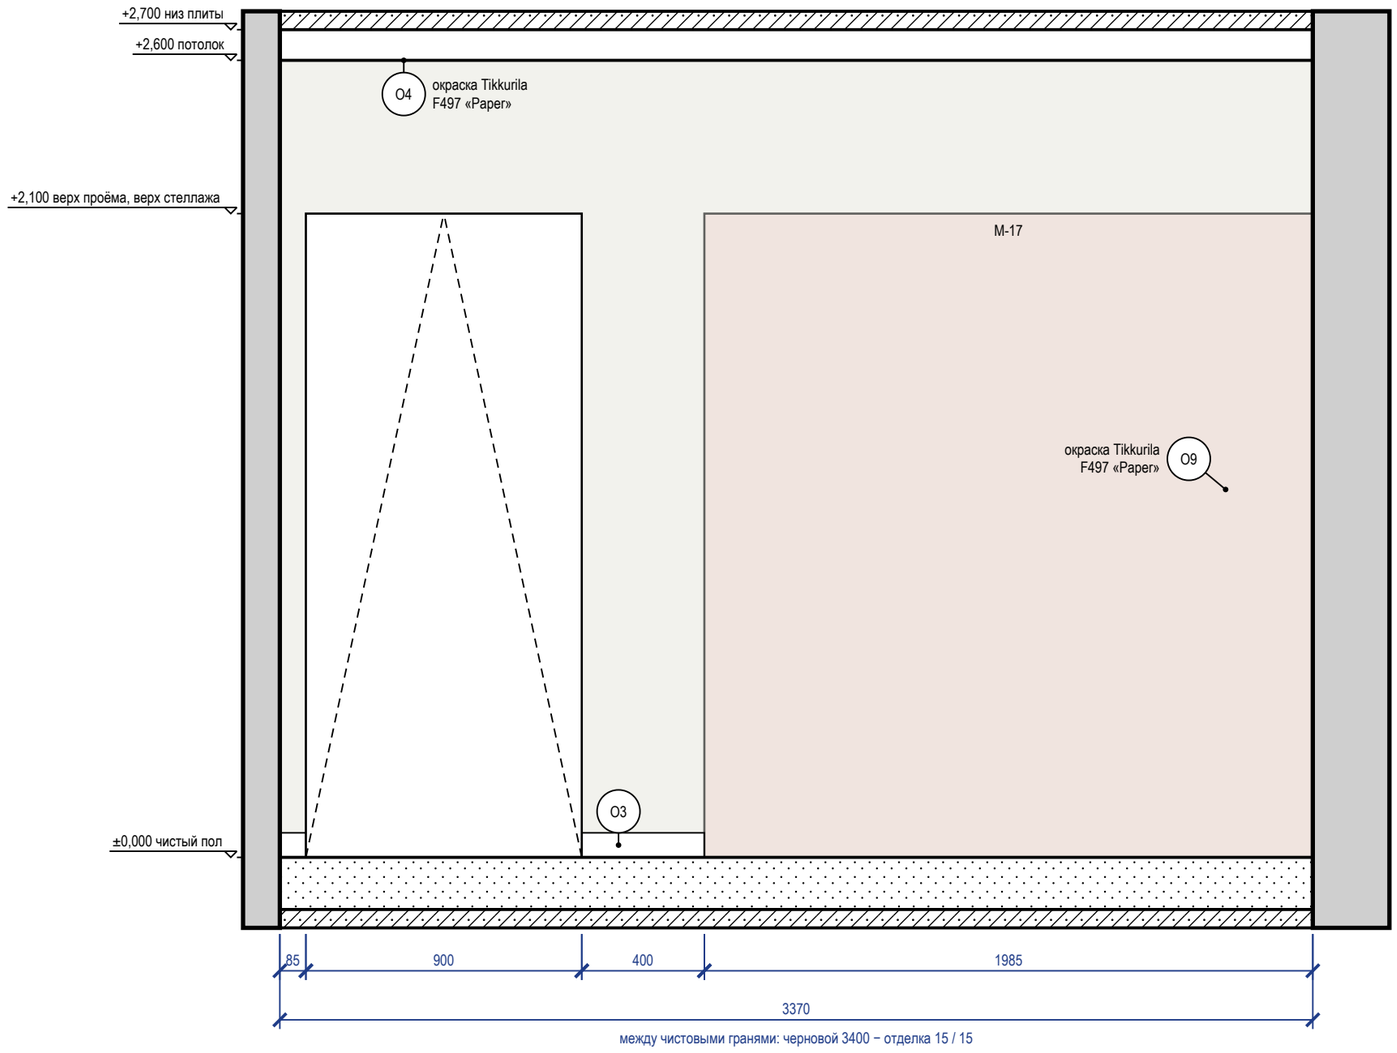


Стена Г — визуализация, лист 10

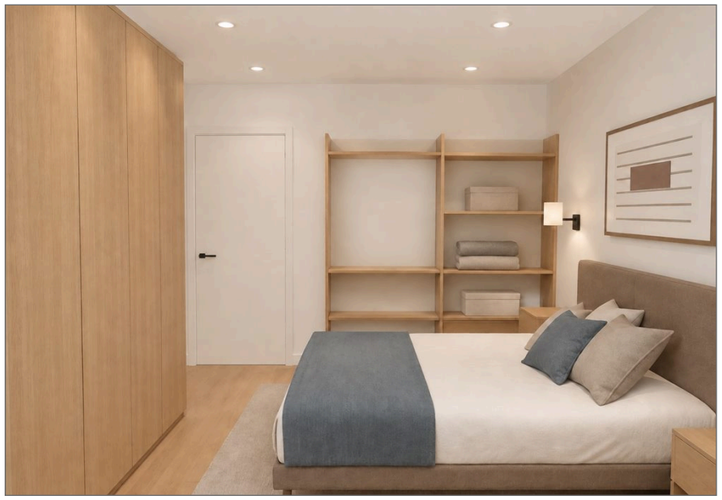

Ведомость отделки (на листе)

Марка	Поверхность	Материал, изделие	Цвет, код	Кол.
О3	плинтус	плинтус МДФ, h 80 мм, аналог: плинтус МДФ под окраску 80×16 мм, полуглянцевая	Tikkurila F497 «Paper»	0,5 м
О4	потолок	окраска, Tikkurila Anti-Reflex 2, глубокоматовая, подготовка Q3	Tikkurila F497 «Paper»	17,5 м²
О9	стены	окраска, Tikkurila Joker, шелковисто-матовая, подготовка К3	Tikkurila F497 «Paper»	6,9 м²

Схема развёрток (М 1:50)

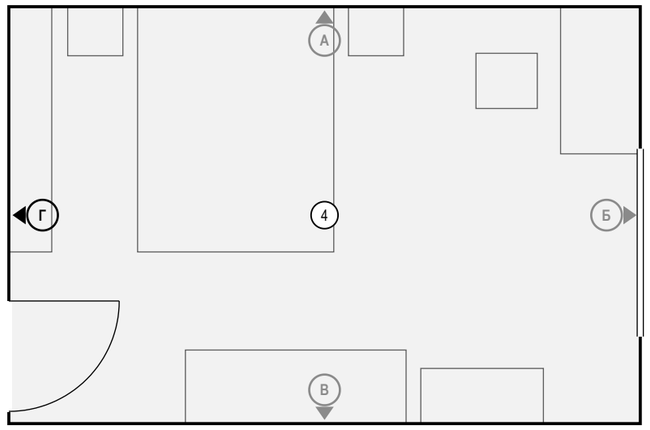


Ведомость изделий и проёмов (на листе)

Марка	Изделие, проём	На виде Ш×В, мм	Низ, мм
М-17	стеллаж книжный открытый	1985×2100	0

5 **Плинтус МДФ 80×16 мм у окрашенной стены по доске (ламинату) (М 1:10)**

Узел 5 — лист С14

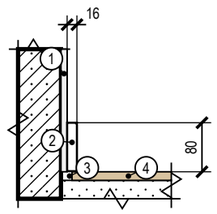

Поз.	Состав слоя, изделие
1	штукатурка, шпаклёвка Q3, окраска — по ведомости отделки
2	плинтус МДФ 80×16 под окраску в цвет стены; клей монтажный — к стене, не к полу
3	зазор покрытия у стены 8–10 мм закрывается плинтусом
4	инженерная доска дуб на клею


Примечания

1. Размеры — в мм от чистовых поверхностей стен; условные обозначения и общие указания — лист 19.

	Лист	№ док.	Подпись	Дата	Проект: Четырёхкомнатная квартира	М 1:20
Дизайнер	Кырлан А.С.			14.11.26	Развёртка стены Г. Детская 1 (пом. 4)	Стадия: П; Лист: 82; Листов: 147
Проверил						
Н. контр.						
Утв.						

выпуск 14.11.2026 № e7147312ff · стр. 82 из 147

Стена А (М 1:20)

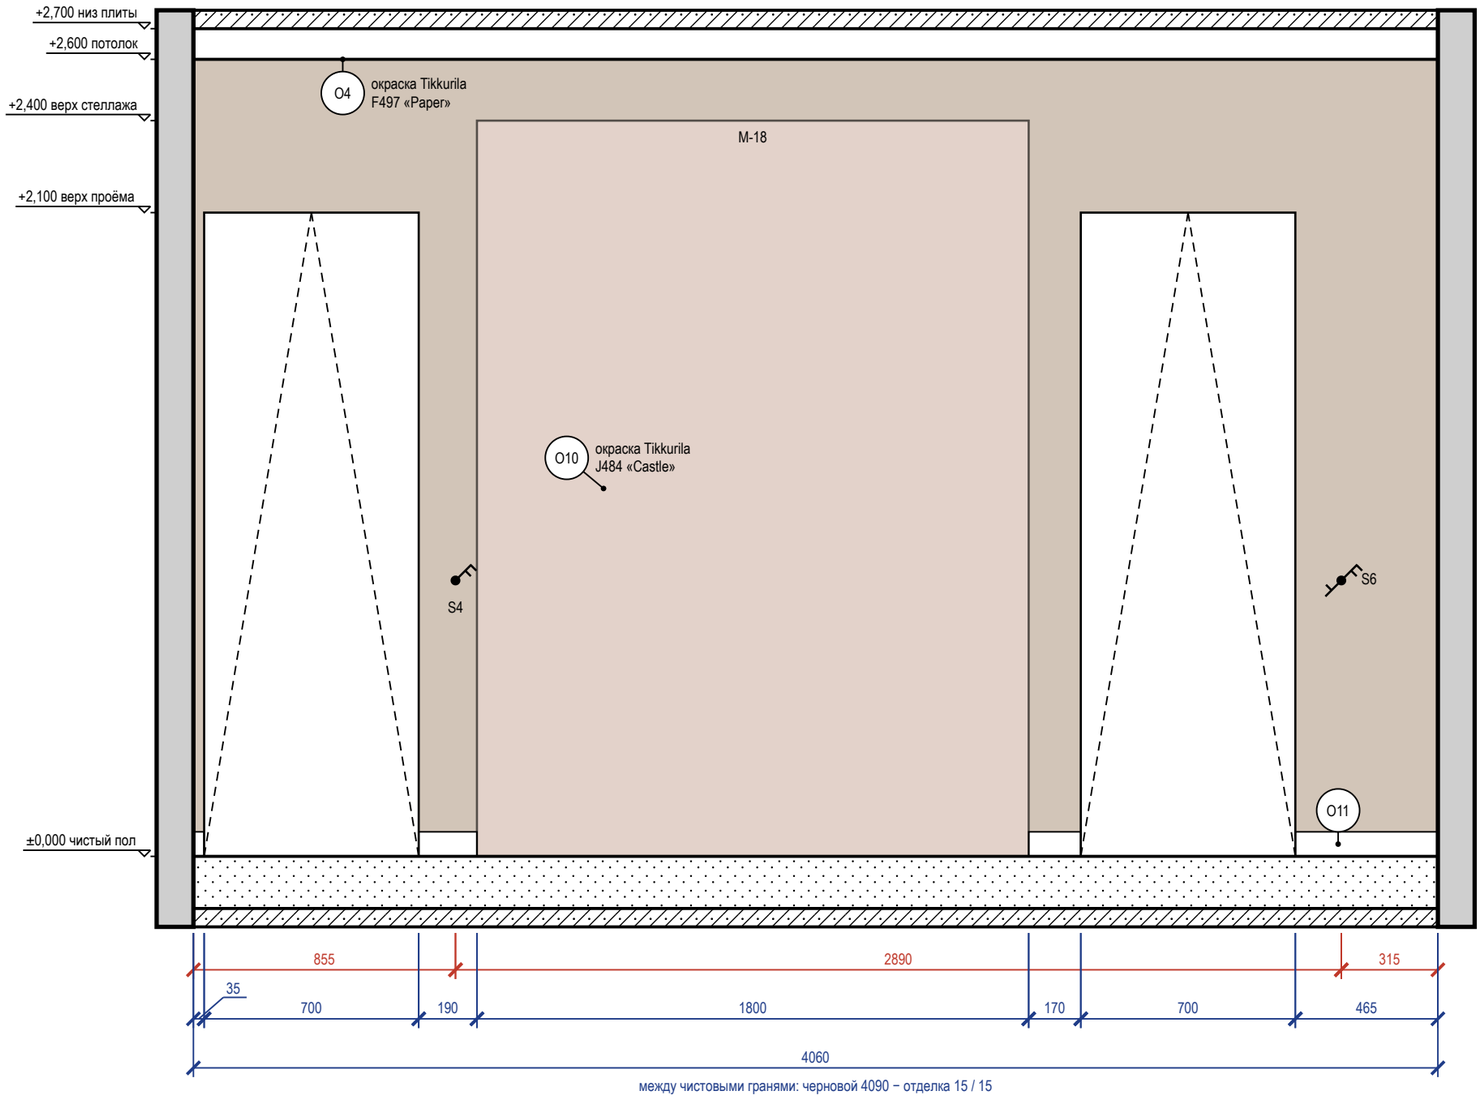


Ведомость отделки (на листе)

Марка	Поверхность	Материал, изделие	Цвет, код	Кол.
O4	потолок	окраска, Tikkurila Anti-Reflex 2, глубокоматовая, подготовка Q3	Tikkurila F497 «Paper»	4,5 м²
O10	стены	окраска, Tikkurila Optiva 20 Semimatt, шелковисто-матовая, подготовка К3	Tikkurila J484 «Castle»	7,6 м²
O11	плинтус	плинтус МДФ, h 80 мм, аналог: плинтус МДФ под окраску 80×16 мм, полуглянцевая	Tikkurila J484 «Castle»	0,9 м

Ведомость точек и выводов

Марка	Что это	Гр.	Н, мм	От угла, мм	Примечание
S4	выключатель	4	900	855	
S6	выключатель	2	900	3745	

Схема развёрток (М 1:50)

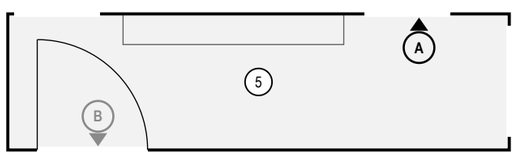

Ведомость изделий и проёмов (на листе)

Марка	Изделие, проём	На виде Ш×В, мм	Низ, мм
M-18	шкаф хозяйственный неглубокий	1800×2400	0


Примечания

1. Размеры — в мм от чистовых поверхностей стен; условные обозначения и общие указания — лист 19.

	Лист	№ док.	Подпись	Дата	Проект: Четырёхкомнатная квартира	М 1:20		
Дизайнер	Кырлан А.С.			14.11.26	Развёртка стены А. Коридор (пом. 5)	Стадия	Лист	Листов
Проверил						П	83	147
Н. контр.								
Утв.								

выпуск 14.11.2026 № e7147312ff · стр. 83 из 147

Стена В (М 1:20)

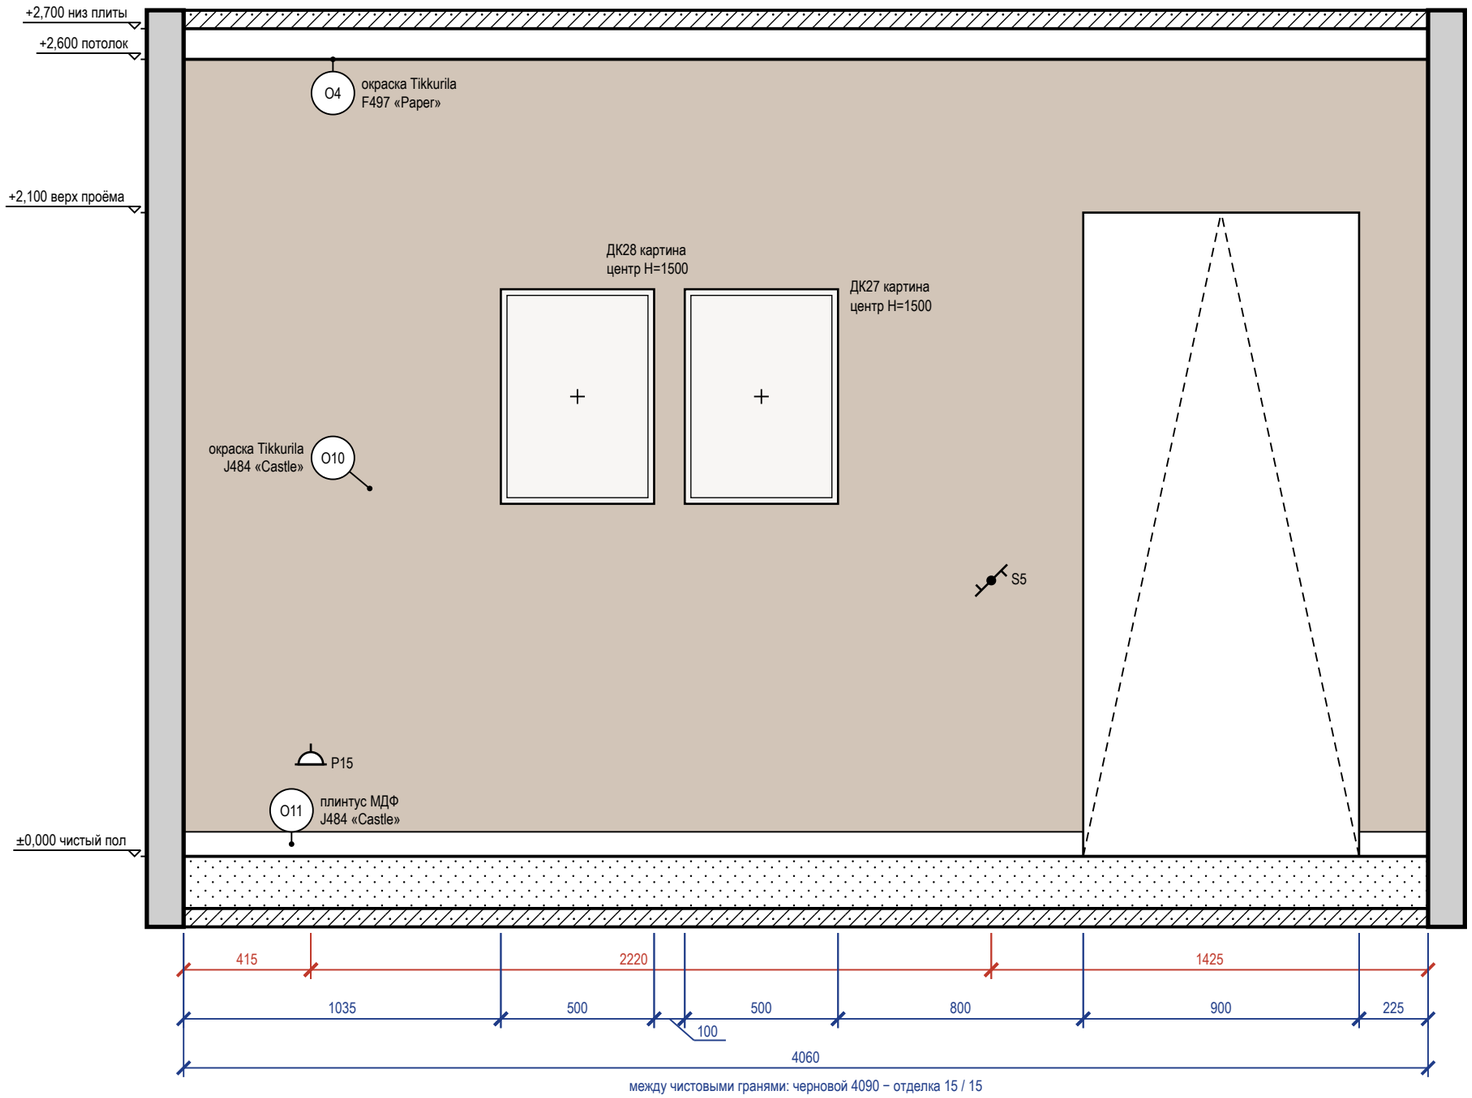

между чистовыми гранями: черновой 4090 − отделка 15 / 15


Ведомость отделки (на листе)

Марка	Поверхность	Материал, изделие	Цвет, код	Кол.
O4	потолок	окраска, Tikkurila Anti-Reflex 2, глубокоматовая, подготовка Q3	Tikkurila F497 «Paper»	4,5 м²
O10	стены	окраска, Tikkurila Optiva 20 Semimatt, шелковисто-матовая, подготовка К3	Tikkurila J484 «Castle»	8,7 м²
O11	плинтус	плинтус МДФ, h 80 мм, аналог: плинтус МДФ под окраску 80×16 мм, полуглянцевая	Tikkurila J484 «Castle»	3,2 м

Ведомость точек и выводов

Марка	Что это	Гр.	H, мм	От угла, мм	Примечание
P15	розетка: уборка	8	300	415	
S5	выключатель	2	900	2635	

Схема развёрток (М 1:50)

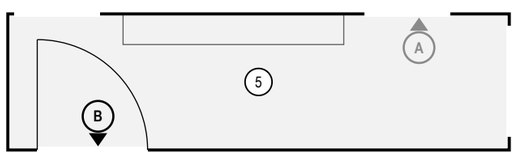

Ведомость изделий и проёмов (на листе)

Марка	Изделие, проём	На виде Ш×В, мм	Низ, мм
ДК28	картина	500×700	1150
ДК27	картина	500×700	1150

Примечания

1. Размеры — в мм от чистовых поверхностей стен; условные обозначения и общие указания — лист 19.
2. Картины и зеркала крепить к основанию по паспорту изделия (закладные и анкеры — в перечне скрытых работ); крест — ось центра предмета.

	Лист	№ док.	Подпись	Дата
Дизайнер	Кырлан А.С.			14.11.26
Проверил				
Н. контр.				
Утв.				


Проект: Четырёхкомнатная квартира — **М 1:20**

Развёртка стены В. Коридор (пом. 5)

Стадия	Лист	Листов
П	84	147

выпуск 14.11.2026 № e7147312ff · стр. 84 из 147

Стена А (М 1:20)

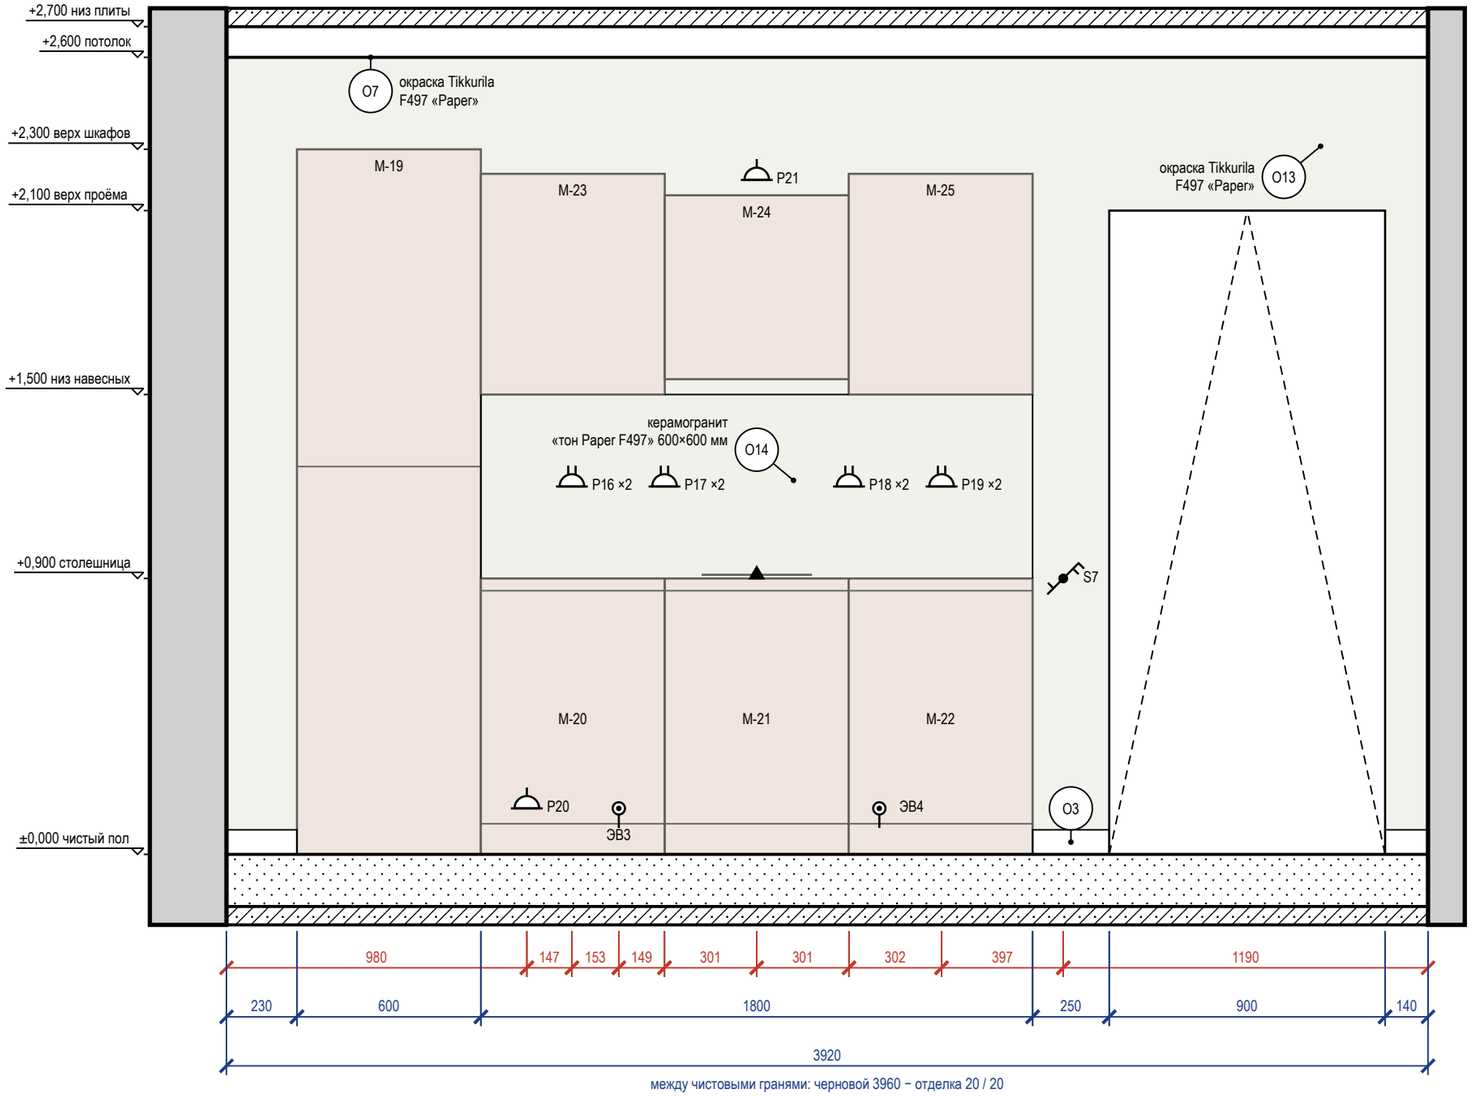

Ведомость точек и выводов

Марка	Что это	Гр.	Н, мм	От угла, мм	Примечание
Р20	розетка: холодильник встроенный М-19 (розетка в модуле М-20)	10	150	980	
Р16	розетка: фартук: мелкая техника	9	1200	1127	рамка 2 поста
ЭВ3	вывод кабеля: варочная панель М-21	11	150	1280	
Р17	розетка: фартук: мелкая техника	9	1200	1429	рамка 2 поста
Р21	розетка: вытяжка М-24 (в модуле, съёмная панель)	10	2200	1730	

Марка	Что это	Гр.	Н, мм	От угла, мм	Примечание
Р18	розетка: фартук: мелкая техника	9	1200	2031	рамка 2 поста
ЭВ4	вывод кабеля: духовой шкаф М-21 (вывод в соседнем модуле М-22)	12	150	2130	
Р19	розетка: фартук: мелкая техника	9	1200	2333	рамка 2 поста
S7	выключатель	1	900	2730	

Примечания

1. Размеры — в мм от чистовых поверхностей стен; условные обозначения и общие указания — лист 19.


Стена А — визуализация, лист 11



Ведомость отделки (на листе)

Марка	Поверхность	Материал, изделие	Цвет, код	Кол.
О3	плинтус	плинтус МДФ, h 80 мм, аналог: плинтус МДФ под окраску 80×16 мм, полуглянцевая	Tikkurila F497 «Paper»	0,6 м
О7	потолок	окраска, Tikkurila Luja 7, матовая, подготовка Q3	Tikkurila F497 «Paper»	15,2 м²
О13	стены	окраска, Tikkurila Luja 7, шелковисто-матовая, подготовка К3	Tikkurila F497 «Paper»	7,2 м²
О14	фартук	керамогранит, 600×600×9 мм, аналог: керамогранит матовый, тон F497, затирка CG2WA	#F1F1EC «тон Paper F497»	1,1 м²

Схема развёрток (М 1:50)

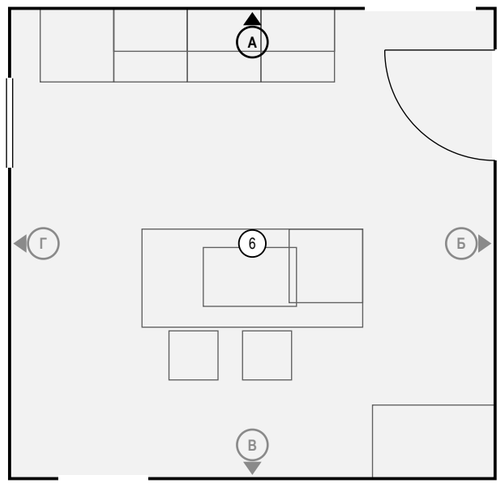

	Лист	№ док.	Подпись	Дата
Дизайнер	Кырлан А.С.			14.11.26
Проверил				
Н. контр.				
Утв.				


Проект: Четырёхкомнатная квартира — **М 1:20**

Развёртка стены А. Кухня (пом. 6), кухонный фронт

Стадия	Лист	Листов
П	85	147

выпуск 14.11.2026 № e7147312ff · стр. 85 из 147

Стена Б (М 1:20)

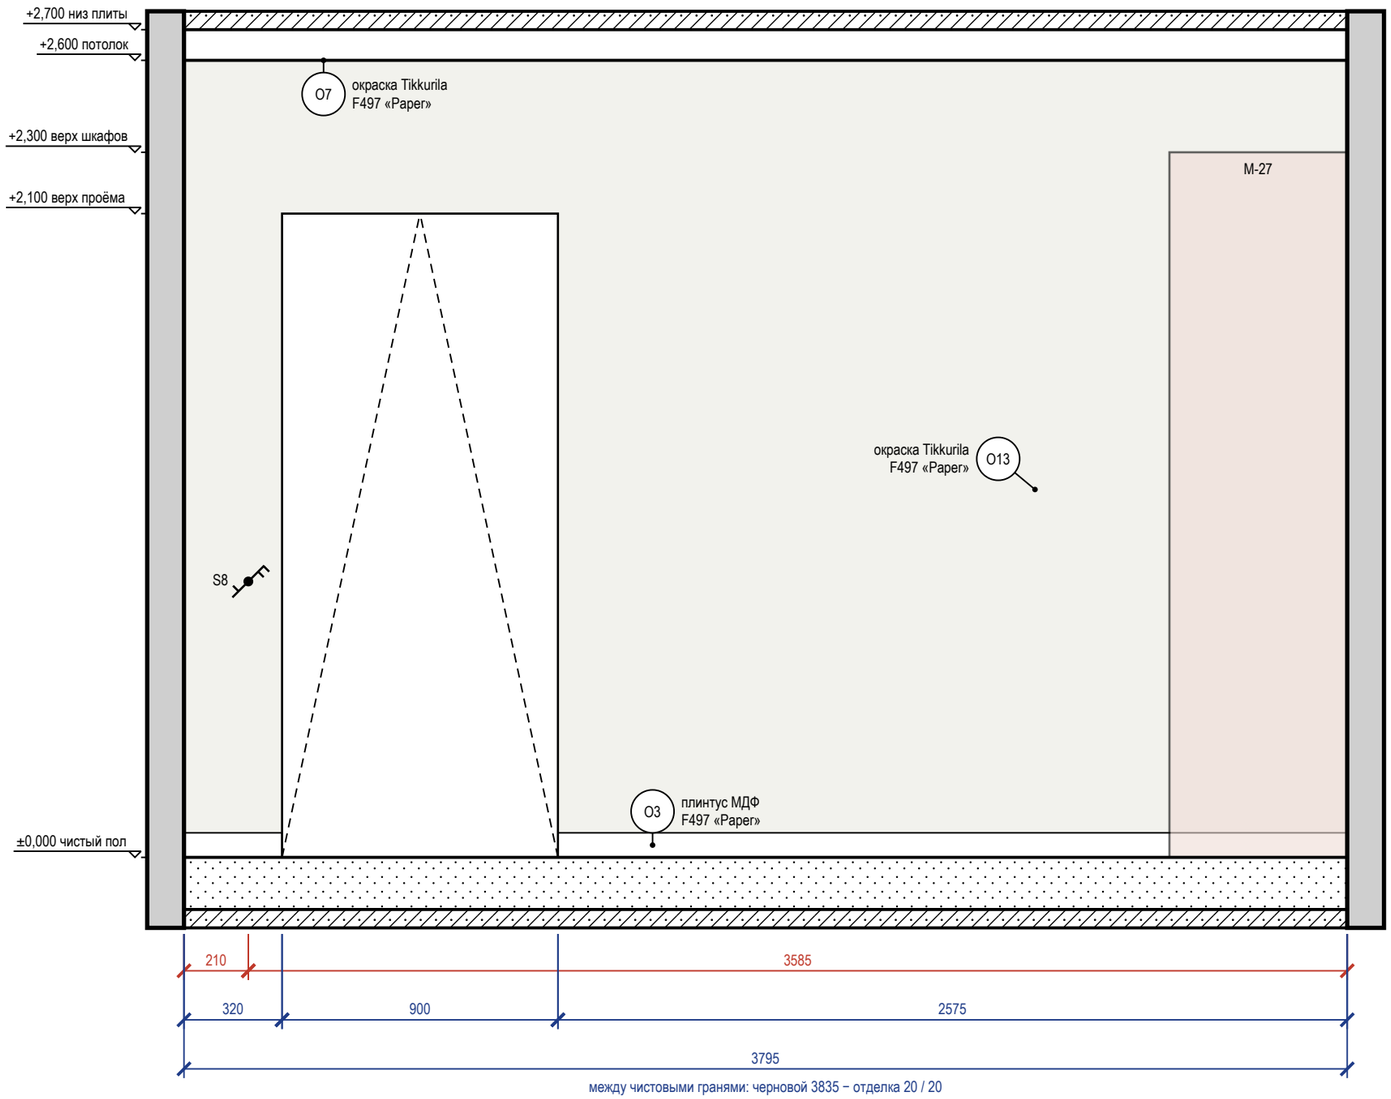

Ведомость точек и выводов

Марка	Что это	Гр.	Н, мм	От угла, мм	Примечание
S8	выключатель	1	900	210	


Ведомость изделий и проёмов (на листе)

Марка	Изделие, проём	На виде Ш×В, мм	Низ, мм
М-27	пенал-кладовая кухонная	580×2300	0

Ведомость отделки (на листе)

Марка	Поверхность	Материал, изделие	Цвет, код	Кол.
О3	плинтус	плинтус МДФ, h 80 мм, аналог: плинтус МДФ под окраску 80×16 мм, полуглянцевая	Tikkurila F497 «Paper»	2,9 м
О7	потолок	окраска, Tikkurila Luja 7, матовая, подготовка Q3	Tikkurila F497 «Paper»	15,2 м²
О13	стены	окраска, Tikkurila Luja 7, шелковисто-матовая, подготовка К3	Tikkurila F497 «Paper»	8 м²

Схема развёрток (М 1:50)

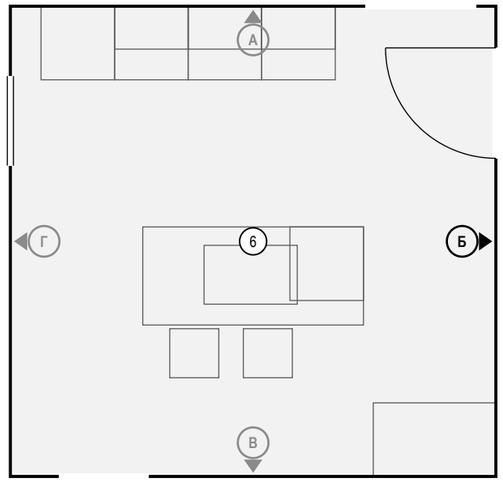

Примечания

1. Размеры — в мм от чистовых поверхностей стен; условные обозначения и общие указания — лист 19.

	Лист	№ док.	Подпись	Дата	Проект: Четырёхкомнатная квартира	М 1:20		
Дизайнер	Кырлан А.С.			14.11.26	Развёртка стены Б. Кухня (пом. 6)	Стадия	Лист	Листов
Проверил						П	86	147
Н. контр.								
Утв.								

Стена В (М 1:20)


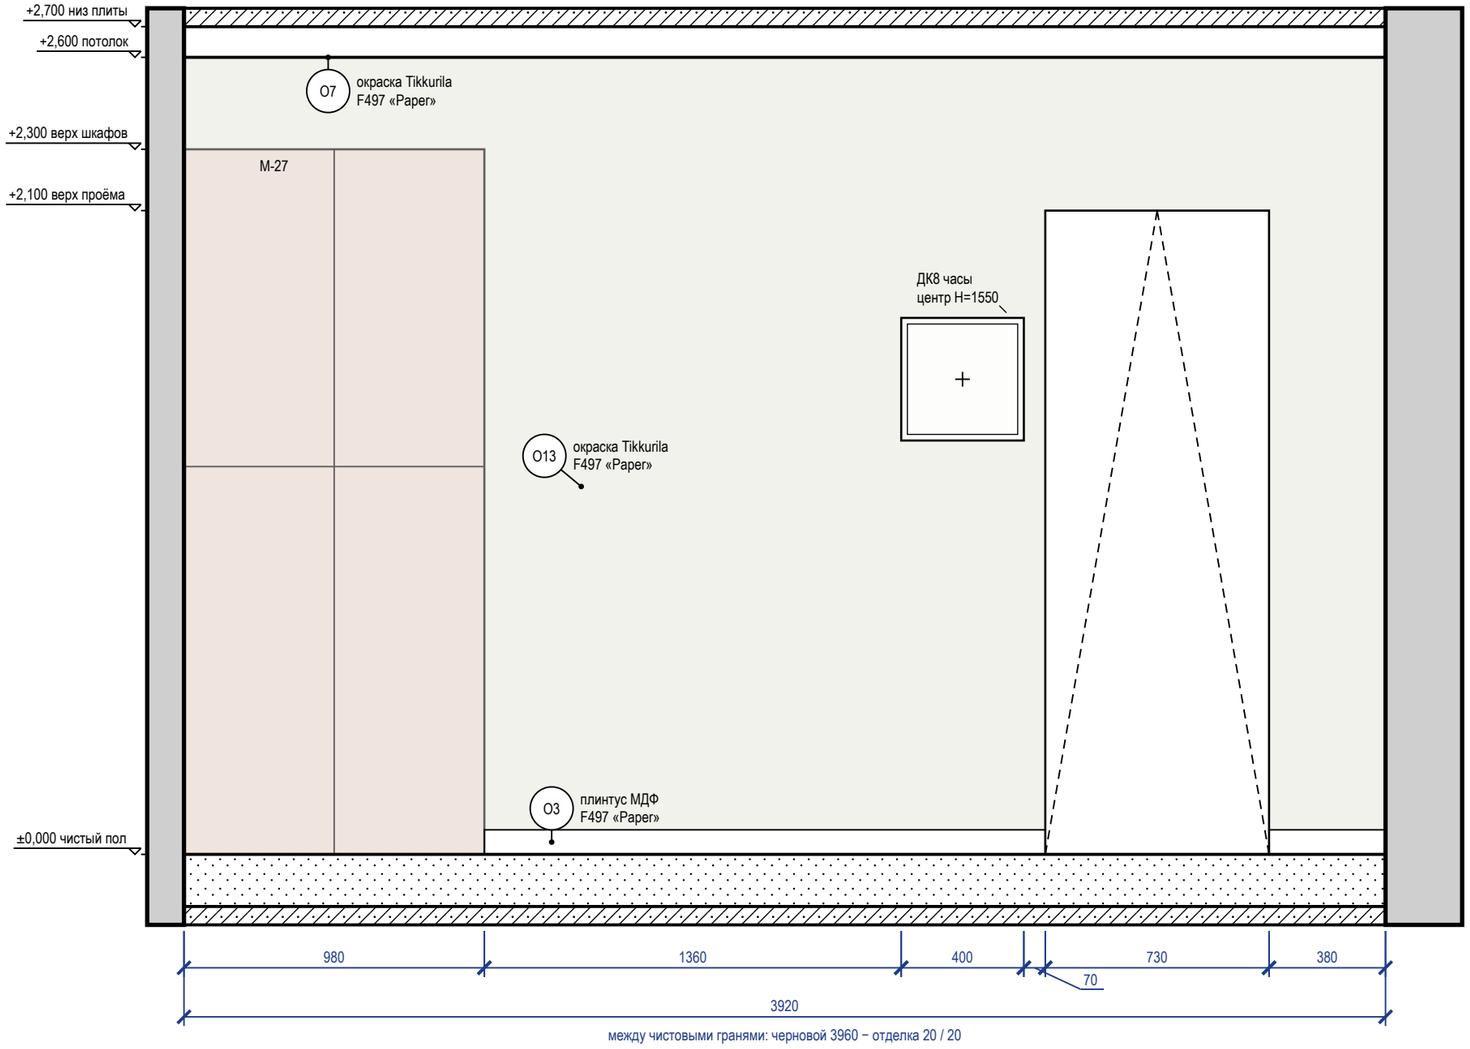


Схема развёрток (М 1:50)

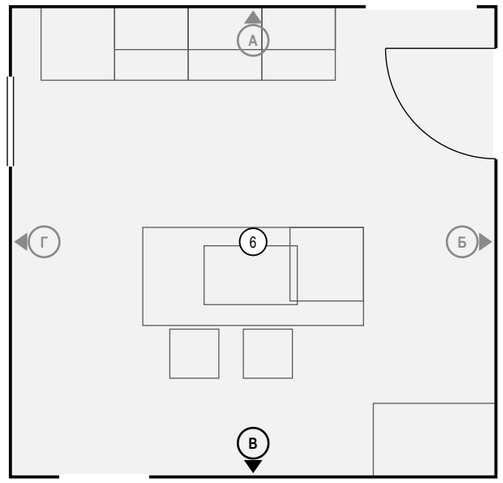


Ведомость отделки (на листе)

Марка	Поверхность	Материал, изделие	Цвет, код	Кол.
О3	плинтус	плинтус МДФ, h 80 мм, аналог: плинтус МДФ под окраску 80×16 мм, полуглянцевая	Tikkurila F497 «Paper»	2,2 м
О7	потолок	окраска, Tikkurila Luja 7, матовая, подготовка Q3	Tikkurila F497 «Paper»	15,2 м²
О13	стены	окраска, Tikkurila Luja 7, шелковисто-матовая, подготовка К3	Tikkurila F497 «Paper»	8,7 м²

Ведомость изделий и проёмов (на листе)

Марка	Изделие, проём	На виде Ш×В, мм	Низ, мм
М-27	пенал-кладовая кухонная	980×2300	0
ДК8	часы	400×400	1350

1 **Порог 15 мм: мокрая зона — смежное помещение (М 1:10)**
Узел 1 — лист С14

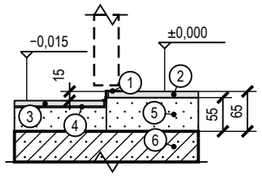

Поз.	Состав слоя, изделие
1	порог-переход металлический, перепад 15 мм, на клей-герметик
2	керамогранит 600×600×10
3	керамогранит 600×600×10
4	гидроизоляция в 2 слоя с подъёмом на торец ступени, лента в углу
5	ЦПС М300 (В22,5) 55 мм; в мокрой зоне 40 мм
6	плита перекрытия

Примечания

1. Размеры — в мм от чистовых поверхностей стен; условные обозначения и общие указания — лист 19.
2. Картины и зеркала крепить к основанию по паспорту изделия (закладные и анкеры — в перечне скрытых работ); крест — ось центра предмета.

	Лист	№ док.	Подпись	Дата
Дизайнер	Кырлан А.С.			14.11.26
Проверил				
Н. контр.				
Утв.				


Проект: Четырёхкомнатная квартира — М 1:20

Развёртка стены В. Кухня (пом. 6)

Стадия	Лист	Листов
П	87	147

выпуск 14.11.2026 № e7147312ff · стр. 87 из 147

Стена Г (М 1:20)

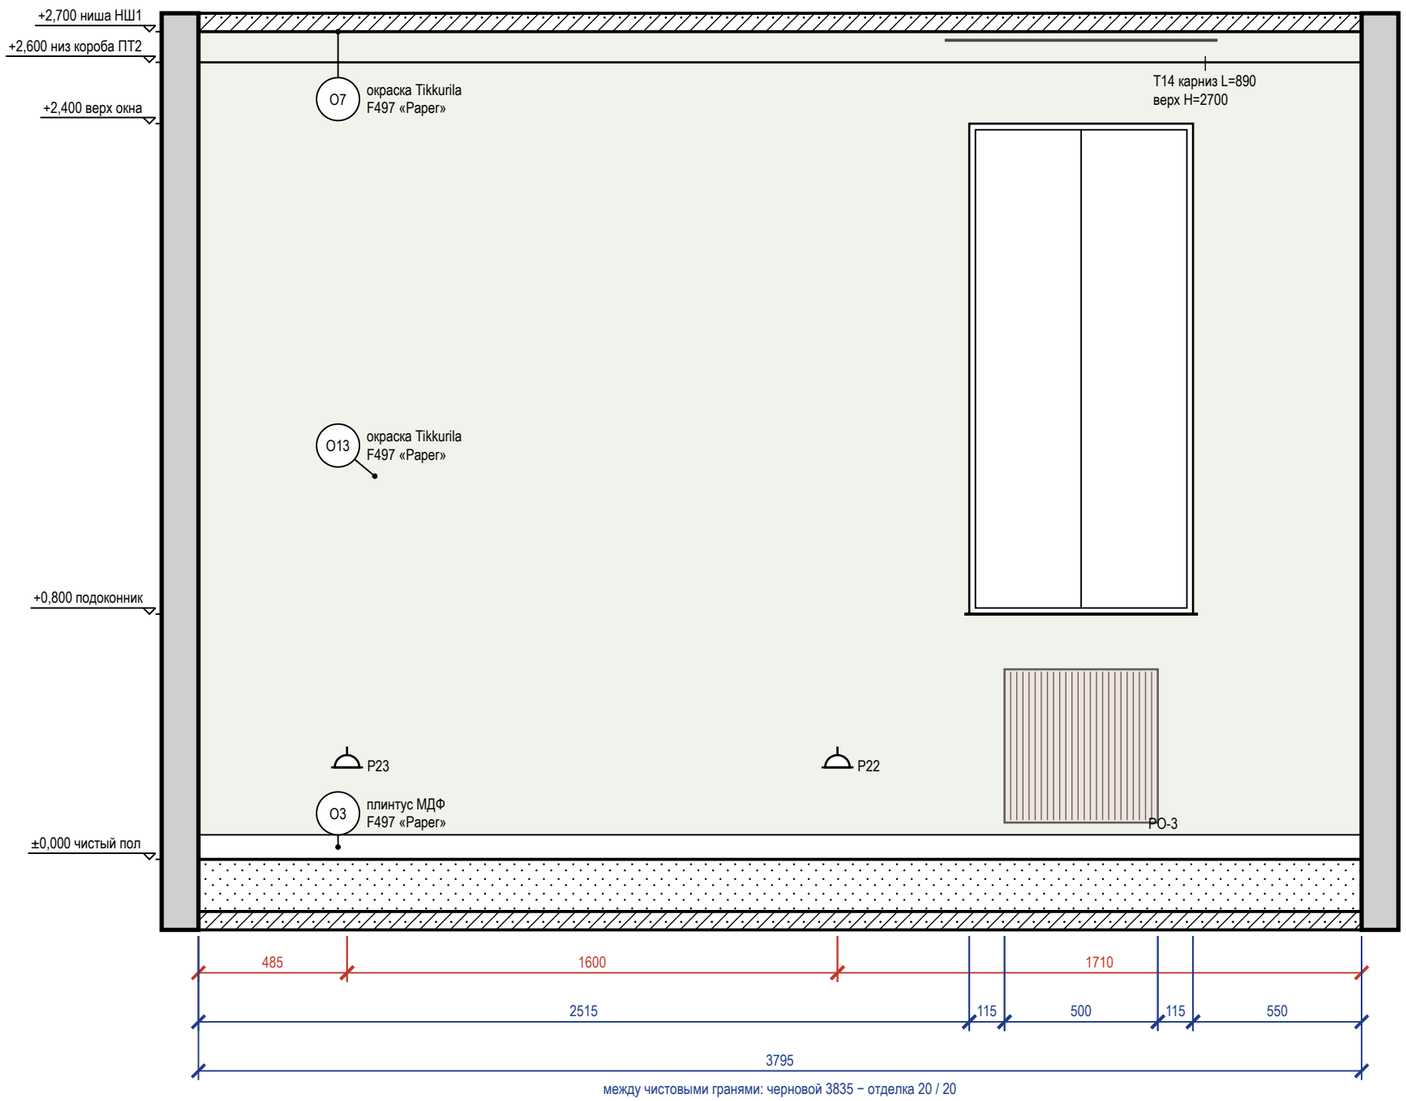


Стена Г — визуализация, лист 12



Ведомость отделки (на листе)

Марка	Поверхность	Материал, изделие	Цвет, код	Кол.
О3	плинтус	плинтус МДФ, h 80 мм, аналог: плинтус МДФ под окраску 80×16 мм, полуглянцевая	Tikkurila F497 «Paper»	3,8 м
О7	потолок	окраска, Tikkurila Luja 7, матовая, подготовка Q3	Tikkurila F497 «Paper»	15,2 м²
О13	стены	окраска, Tikkurila Luja 7, шелковисто-матовая, подготовка К3	Tikkurila F497 «Paper»	9,1 м²

Схема развёрток (М 1:50)

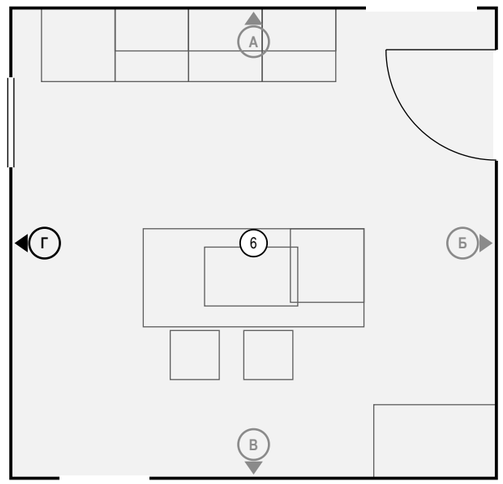

Ведомость точек и выводов

Марка	Что это	Гр.	Н, мм	От угла, мм	Примечание
Р23	розетка: уборка	10	300	485	
Р22	розетка: кухня: мелкая техника	10	300	2085	

Ведомость изделий и проёмов (на листе)

Марка	Изделие, проём	На виде Ш×В, мм	Низ, мм
РО-3	радиатор отопления	500×500	120

Примечания

1. Размеры — в мм от чистовых поверхностей стен; условные обозначения и общие указания — лист 19.
2. Карнизы (шины) — по ведомости текстиля декоратора: длина L и верх H на развёртке — те же числа, что в ведомости; крепление — до окраски потолка.

	Лист	№ док.	Подпись	Дата
Дизайнер	Кырлан А.С.			14.11.26
Проверил				
Н. контр.				
Утв.				


Проект: Четырёхкомнатная квартира — М 1:20

Развёртка стены Г. Кухня (пом. 6)

Стадия	Лист	Листов
П	88	147

выпуск 14.11.2026 № e7147312ff · стр. 88 из 147

Стена А (М 1:20)

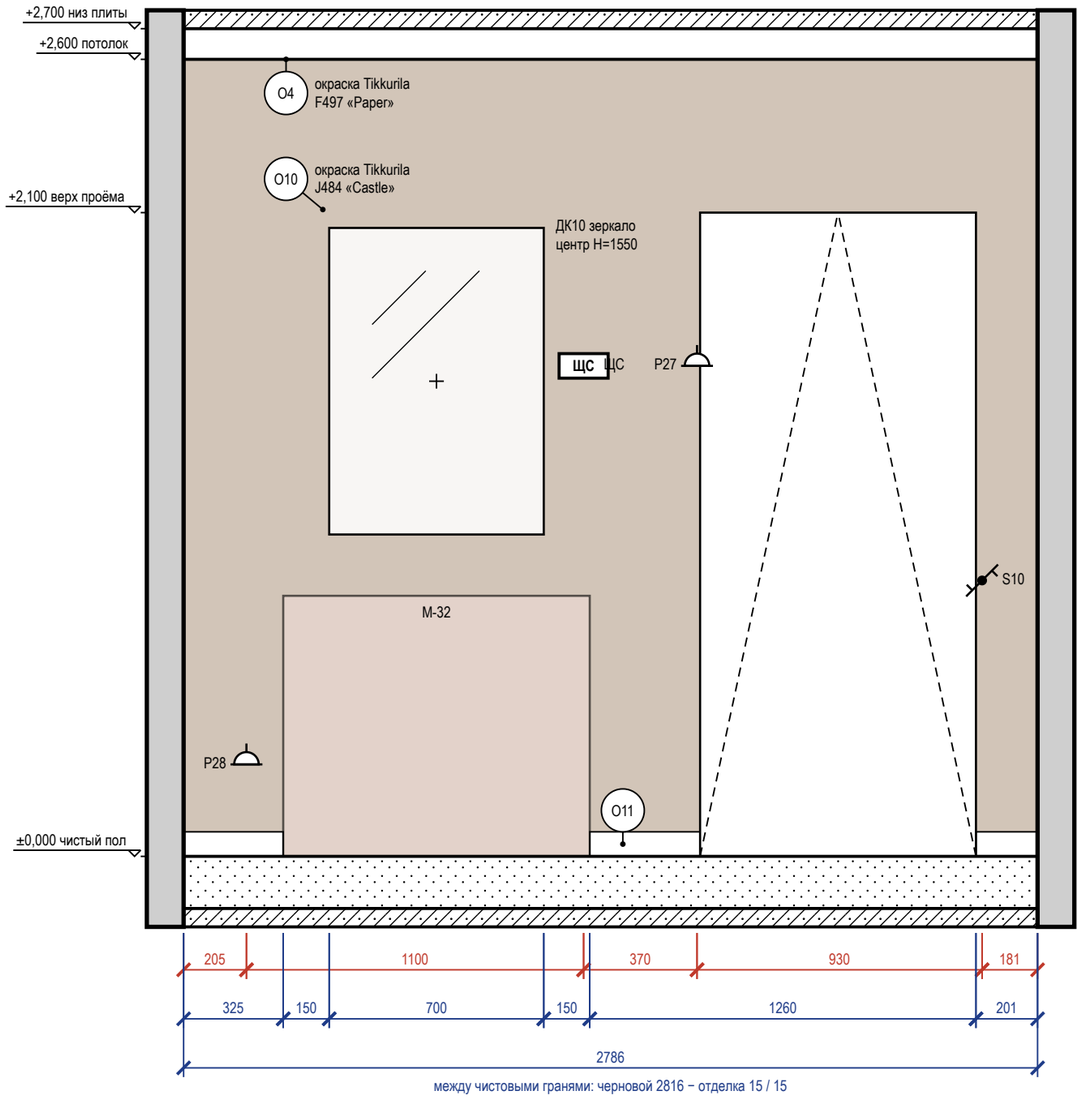

Ведомость отделки (на листе)

Марка	Поверхность	Материал, изделие	Цвет, код	Кол.
О4	потолок	окраска, Tikkurila Anti-Reflex 2, глубокоматовая, подготовка Q3	Tikkurila F497 «Paper»	7,8 м²
О10	стены	окраска, Tikkurila Optiva 20 Semimatt, шелковисто-матовая, подготовка К3	Tikkurila J484 «Castle»	5,4 м²
О11	плинтус	плинтус МДФ, h 80 мм, аналог: плинтус МДФ под окраску 80×16 мм, полуглянцевая	Tikkurila J484 «Castle»	0,9 м

Примечания

1. Размеры — в мм от чистовых поверхностей стен; условные обозначения и общие указания — лист 19.
2. Картины и зеркала крепить к основанию по паспорту изделия (закладные и анкеры — в перечне скрытых работ); крест — ось центра предмета.


Ведомость точек и выводов

Марка	Что это	Гр.	Н, мм	От угла, мм	Примечание
Р28	розетка: уборка	8	300	205	
ЩС	щит: слаботочный щит ЩС (медиащит): роутер, ONT, коммутатор PoE		1600	1305	
Р27	розетка: слаботочный щит ЩС: роутер, ONT	18	1600	1675	
S10	выключатель	2	900	2605	

Стена А — визуализация, лист 13



Схема развёрток (М 1:50)

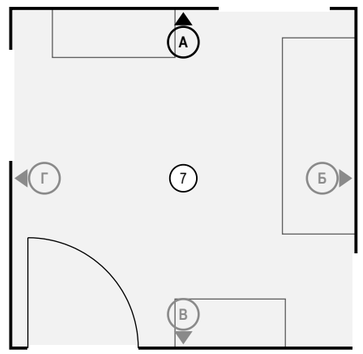


Ведомость изделий и проёмов (на листе)

Марка	Изделие, проём	На виде Ш×В, мм	Низ, мм
М-32	консоль прихожей, 3 ящика	1000×850	0
ДК10	зеркало	700×1000	1050

	Лист	№ док.	Подпись	Дата	Проект: Четырёхкомнатная квартира	М 1:20		
Дизайнер	Кырлан А.С.			14.11.26	Развёртка стены А. Прихожая-коридор (пом. 7)	Стадия	Лист	Листов
Проверил						П	89	147
Н. контр.								
Утв.								

выпуск 14.11.2026 № e7147312ff · стр. 89 из 147

Стена Б (М 1:20)

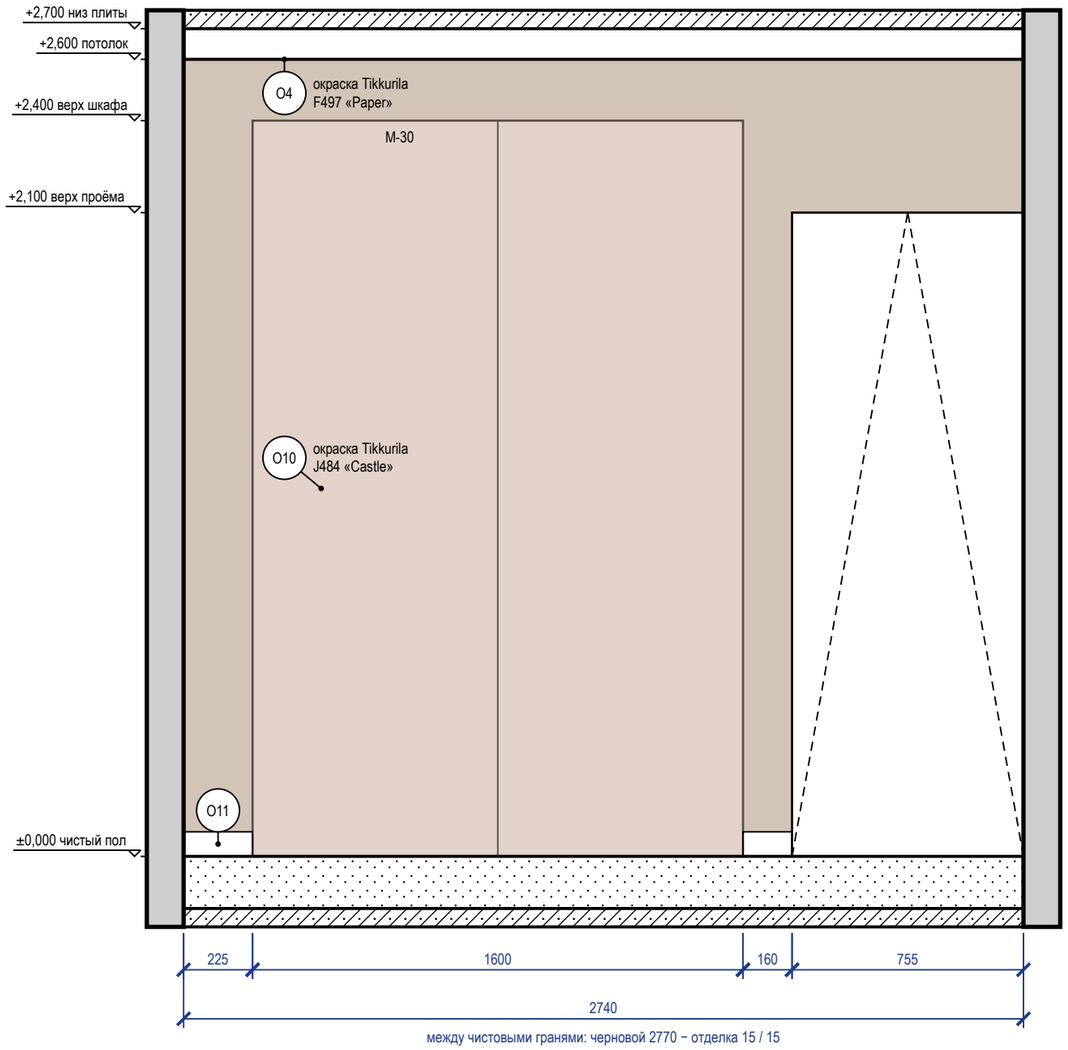


Ведомость изделий и проёмов (на листе)

Марка	Изделие, проём	На виде Ш×В, мм	Низ, мм
М-30	шкаф-купе, 2 двери	1600×2400	0

Ведомость отделки (на листе)


Марка	Поверхность	Материал, изделие	Цвет, код	Кол.
O4	потолок	окраска, Tikkurila Anti-Reflex 2, глубокоматовая, подготовка Q3	Tikkurila F497 «Paper»	7,8 м²
O10	стены	окраска, Tikkurila Optiva 20 Semimatt, шелковисто-матовая, подготовка К3	Tikkurila J484 «Castle»	5,5 м²
O11	плинтус	плинтус МДФ, h 80 мм, аналог: плинтус МДФ под окраску 80×16 мм, полуглянцевая	Tikkurila J484 «Castle»	0,4 м

Схема развёрток (М 1:50)

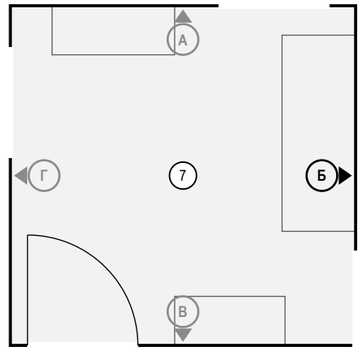

6 **Плинтус МДФ 80×16 мм у окрашенной стены по керамограниту (плитке) (М 1:10)**

Узел 6 — лист С14

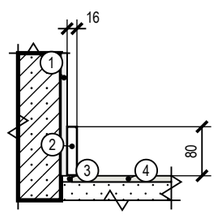

Поз.	Состав слоя, изделие
1	штукатурка, шпаклёвка Q3, окраска — по ведомости отделки
2	плинтус МДФ 80×16 под окраску в цвет стены; клей монтажный — к стене, не к полу
3	зазор покрытия у стены 8–10 мм закрывается плинтусом
4	керамогранит 600×600×10


Примечания

1. Размеры — в мм от чистовых поверхностей стен; условные обозначения и общие указания — лист 19.
2. Дверь заходит за угол помещения: на развёртке показана видимая часть проёма 770 из 900 мм — проверить привязку двери в модели.

	Лист	№ док.	Подпись	Дата	Проект: Четырёхкомнатная квартира			М 1:20
Дизайнер	Кырлан А.С.			14.11.26	Развёртка стены Б. Прихожая-коридор (пом. 7)	Стадия	Лист	Листов
Проверил						П	90	147
Н. контр.								
Утв.								


выпуск 14.11.2026 № e7147312ff · стр. 90 из 147

Стена В (М 1:20)

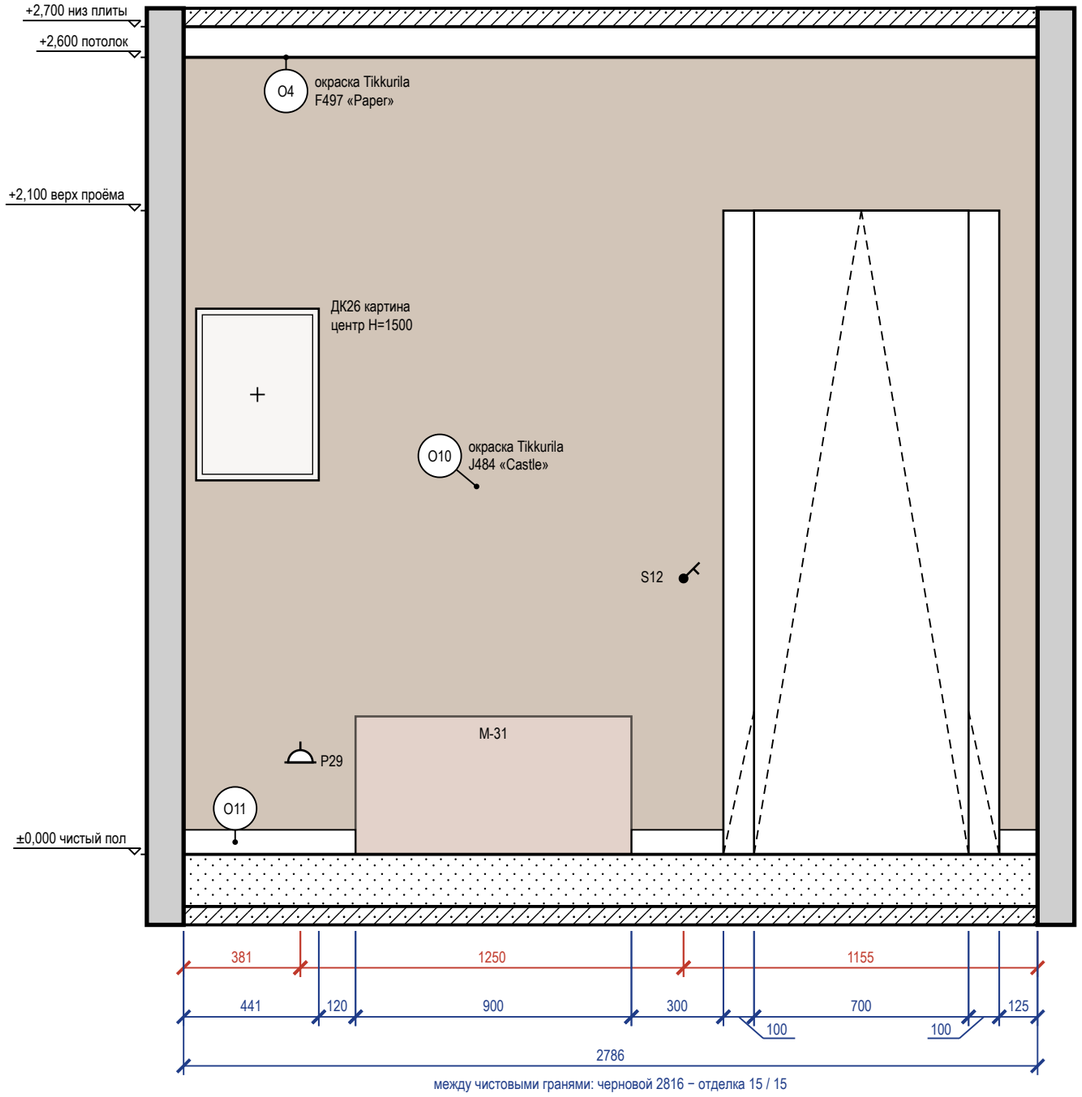

между чистовыми гранями: черновой 2816 − отделка 15 / 15

Стена Г (М 1:20)

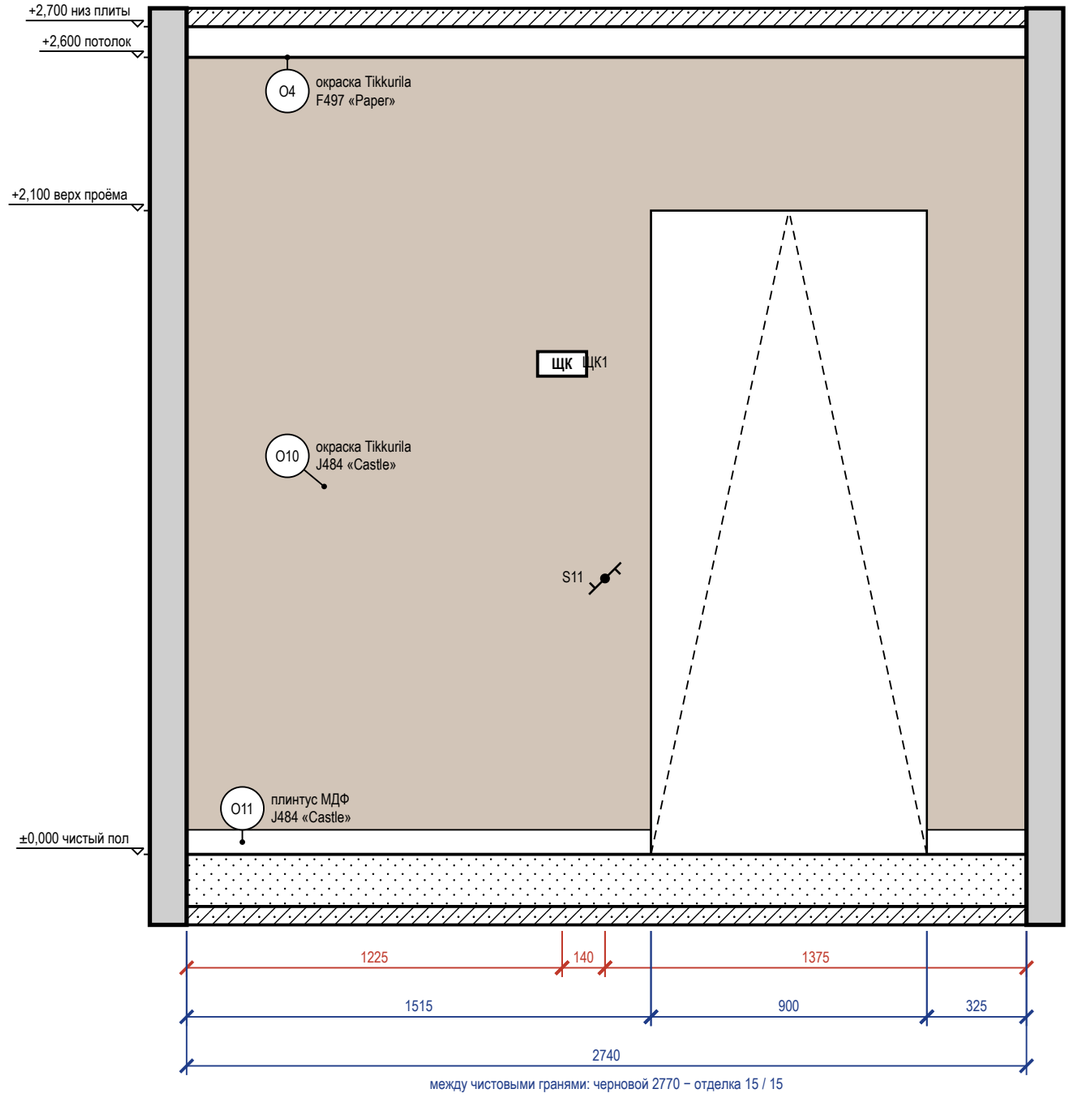

между чистовыми гранями: черновой 2770 − отделка 15 / 15


Ведомость точек и выводов

Стена	Марка	Что это	Гр.	H, мм	От угла, мм	Примечание
В	Р29	розетка: уборка	8	300	381	
В	S12	выключатель	2	900	1631	
Г	ЩК1	щит: квартирный щит ЩК, 72 модуля		1600	1225	
Г	S11	выключатель	2	900	1365	

Ведомость отделки (на листе)

Марка	Поверхность	Материал, изделие	Цвет, код	Кол.
О4	потолок	окраска, Tikkurila Anti-Reflex 2, глубокоматовая, подготовка Q3	Tikkurila F497 «Paper»	7,8 м²
О10	стены	окраска, Tikkurila Optiva 20 Semimatt, шелковисто-матовая, подготовка К3	Tikkurila J484 «Castle»	9,1 м²
О11	плинтус	плинтус МДФ, h 80 мм, аналог: плинтус МДФ под окраску 80×16 мм, полуглянцевая	Tikkurila J484 «Castle»	2,8 м

Схема развёрток (М 1:100)

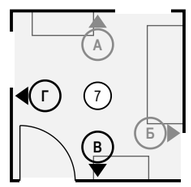

Примечания

1. Размеры — в мм от чистовых поверхностей стен; условные обозначения и общие указания — лист 19.
2. Картины и зеркала крепить к основанию по паспорту изделия (закладные и анкеры — в перечне скрытых работ); крест — ось центра предмета.

	Лист	№ док.	Подпись	Дата
Дизайнер	Кырлан А.С.			14.11.26
Проверил				
Н. контр.				
Утв.				


Проект: Четырёхкомнатная квартира — М 1:20

Развёртки стен В, Г. Прихожая-коридор (пом. 7)


Стадия	Лист	Листов
П	91	147

выпуск 14.11.2026 № e7147312ff · стр. 91 из 147


Стена А (М 1:20)

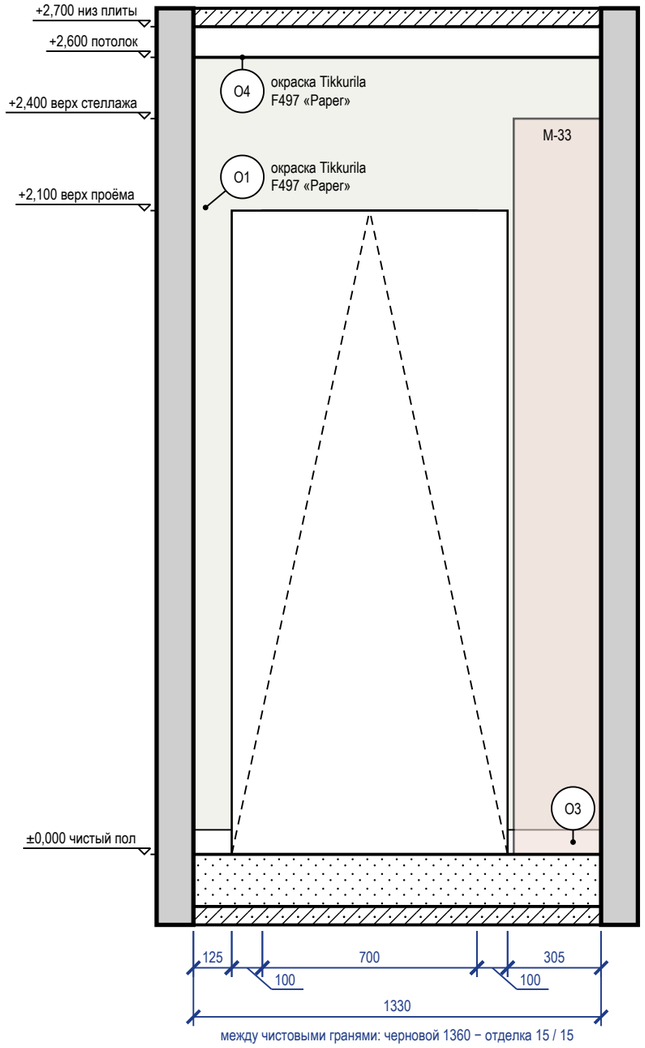

Стена Б (М 1:20)

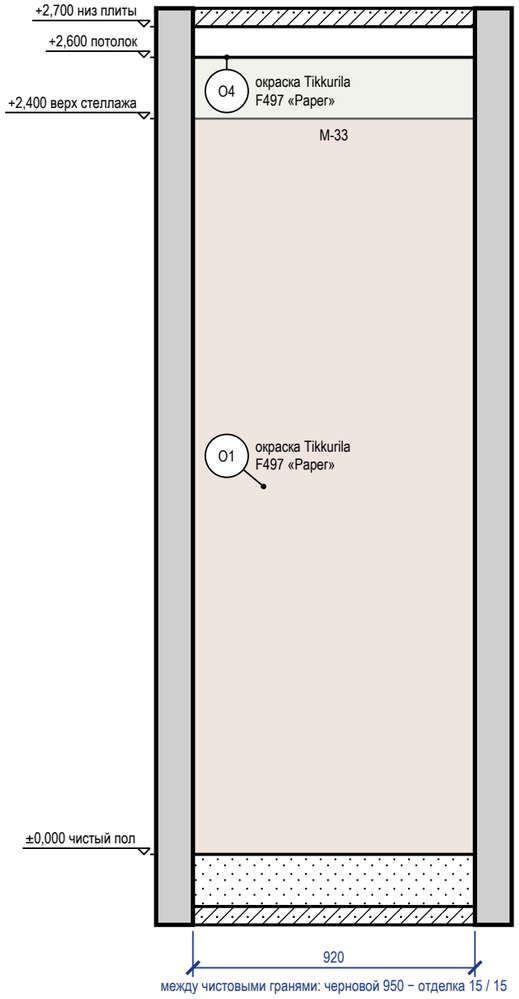


Стена Г (М 1:20)

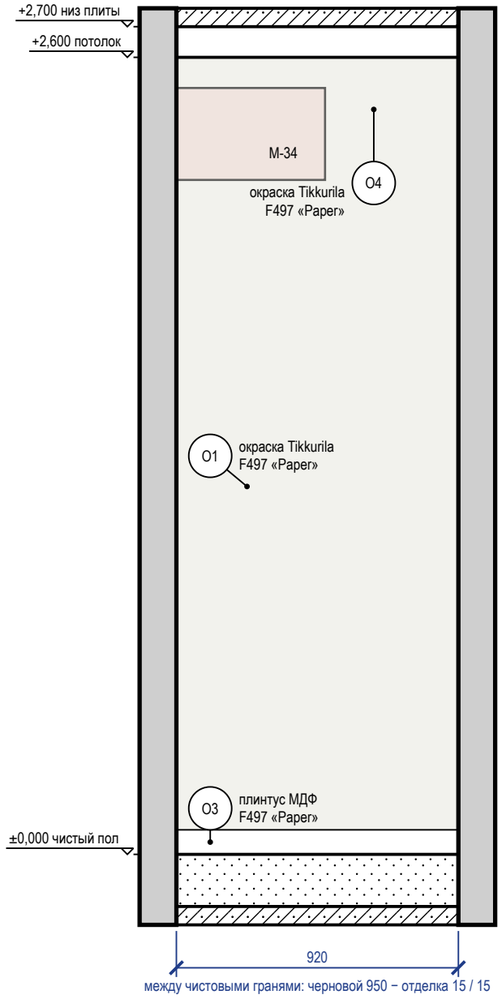

Ведомость отделки (на листе)

Марка	Поверхность	Материал, изделие	Цвет, код	Кол.
О1	стены	окраска, Tikkurila Optiva 5 Matt, матовая, подготовка К3	Tikkurila F497 «Paper»	4,9 м²
О3	плинтус	плинтус МДФ, h 80 мм, аналог: плинтус МДФ под окраску 80×16 мм, полуглянцевая	Tikkurila F497 «Paper»	1,4 м
О4	потолок	окраска, Tikkurila Anti-Reflex 2, глубокоматовая, подготовка Q3	Tikkurila F497 «Paper»	1,3 м²

Схема развёрток (М 1:50)

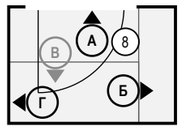

Ведомость изделий и проёмов (на листе)

Стена	Марка	Изделие, проём	На виде Ш×В, мм	Низ, мм
А	М-33	система хранения: штанга, полки, ящики	285×2400	0
Б	М-33	система хранения: штанга, полки, ящики	920×2400	0
Г	М-34	антресоль над зоной открывания двери	485×300	2200


Примечания

1. Размеры — в мм от чистовых поверхностей стен; условные обозначения и общие указания — лист 19.


	Лист	№ док.	Подпись	Дата	Проект: Четырёхкомнатная квартира	М 1:20		
Дизайнер	Кырлан А.С.			14.11.26	Развёртки стен А, Б, Г. Гардеробная 2 (пом. 8)	Стадия	Лист	Листов
Проверил						П	92	147
Н. контр.								
Утв.								

выпуск 14.11.2026 № e7147312ff · стр. 92 из 147

Стена В (М 1:20)

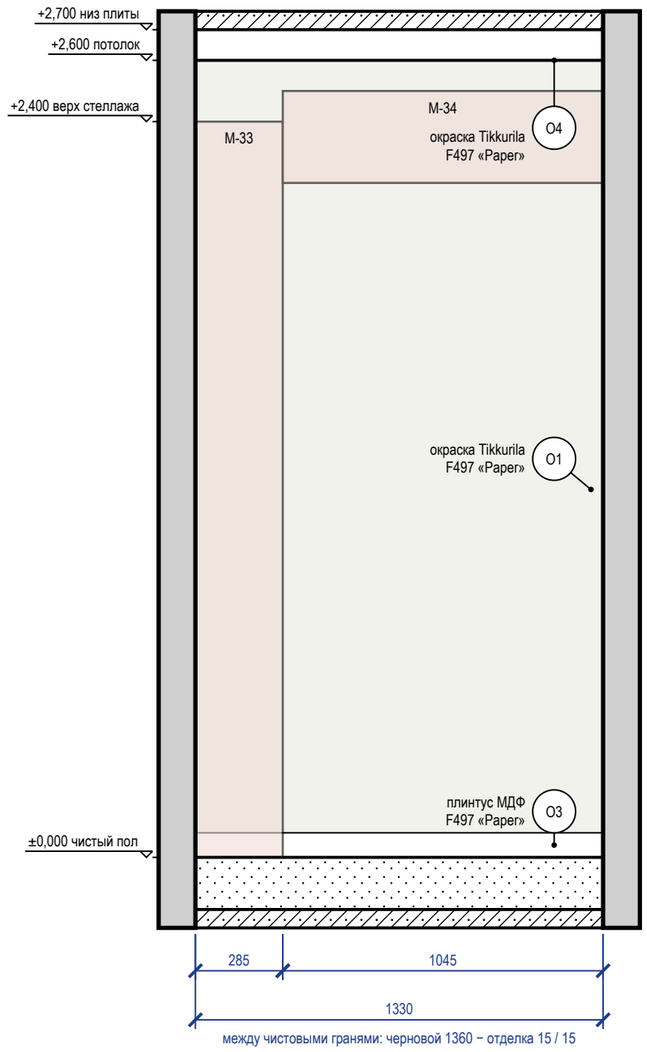


Стена В — визуализация, лист 14

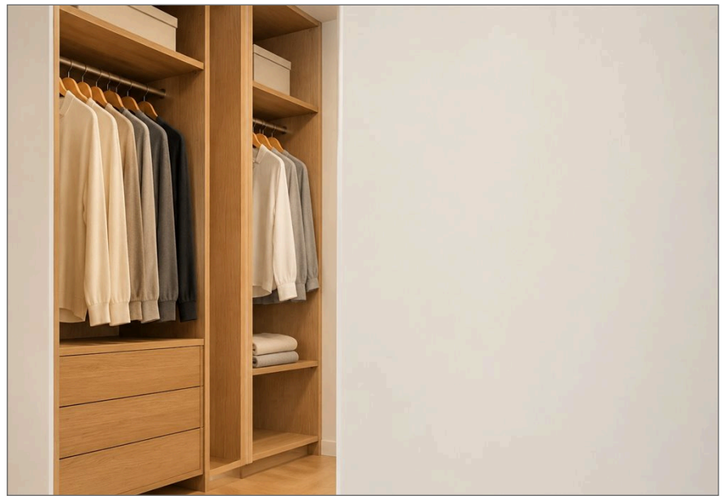

Ведомость отделки (на листе)

Марка	Поверхность	Материал, изделие	Цвет, код	Кол.
О1	стены	окраска, Tikkurila Optiva 5 Matt, матовая, подготовка К3	Tikkurila F497 «Paperi»	3,5 м²
О3	плинтус	плинтус МДФ, h 80 мм, аналог: плинтус МДФ под окраску 80×16 мм, полуглянцевая	Tikkurila F497 «Paperi»	1,3 м
О4	потолок	окраска, Tikkurila Anti-Reflex 2, глубокоматовая, подготовка Q3	Tikkurila F497 «Paperi»	1,3 м²

Схема развёрток (М 1:50)

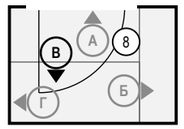


Ведомость изделий и проёмов (на листе)

Марка	Изделие, проём	На виде Ш×В, мм	Низ, мм
М-33	система хранения: штанга, полки, ящики	285×2400	0
М-34	антресоль над зоной открывания двери	1045×300	2200

5 **Плинтус МДФ 80×16 мм у окрашенной стены по доске (ламинату) (М 1:10)**

Узел 5 — лист С14

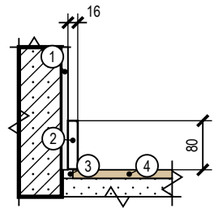

Поз.	Состав слоя, изделие
1	штукатурка, шпаклёвка Q3, окраска — по ведомости отделки
2	плинтус МДФ 80×16 под окраску в цвет стены; клей монтажный — к стене, не к полу
3	зазор покрытия у стены 8–10 мм закрывается плинтусом
4	инженерная доска дуб на клею

Примечания

1. Размеры — в мм от чистовых поверхностей стен; условные обозначения и общие указания — лист 19.

	Лист	№ док.	Подпись	Дата
Дизайнер	Кырлан А.С.			14.11.26
Проверил				
Н. контр.				
Утв.				


Проект: Четырёхкомнатная квартира — **М 1:20**

Развёртка стены В. Гардеробная 2 (пом. 8)

Стадия	Лист	Листов
П	93	147

выпуск 14.11.2026 № e7147312ff · стр. 93 из 147

Стена А (М 1:20)

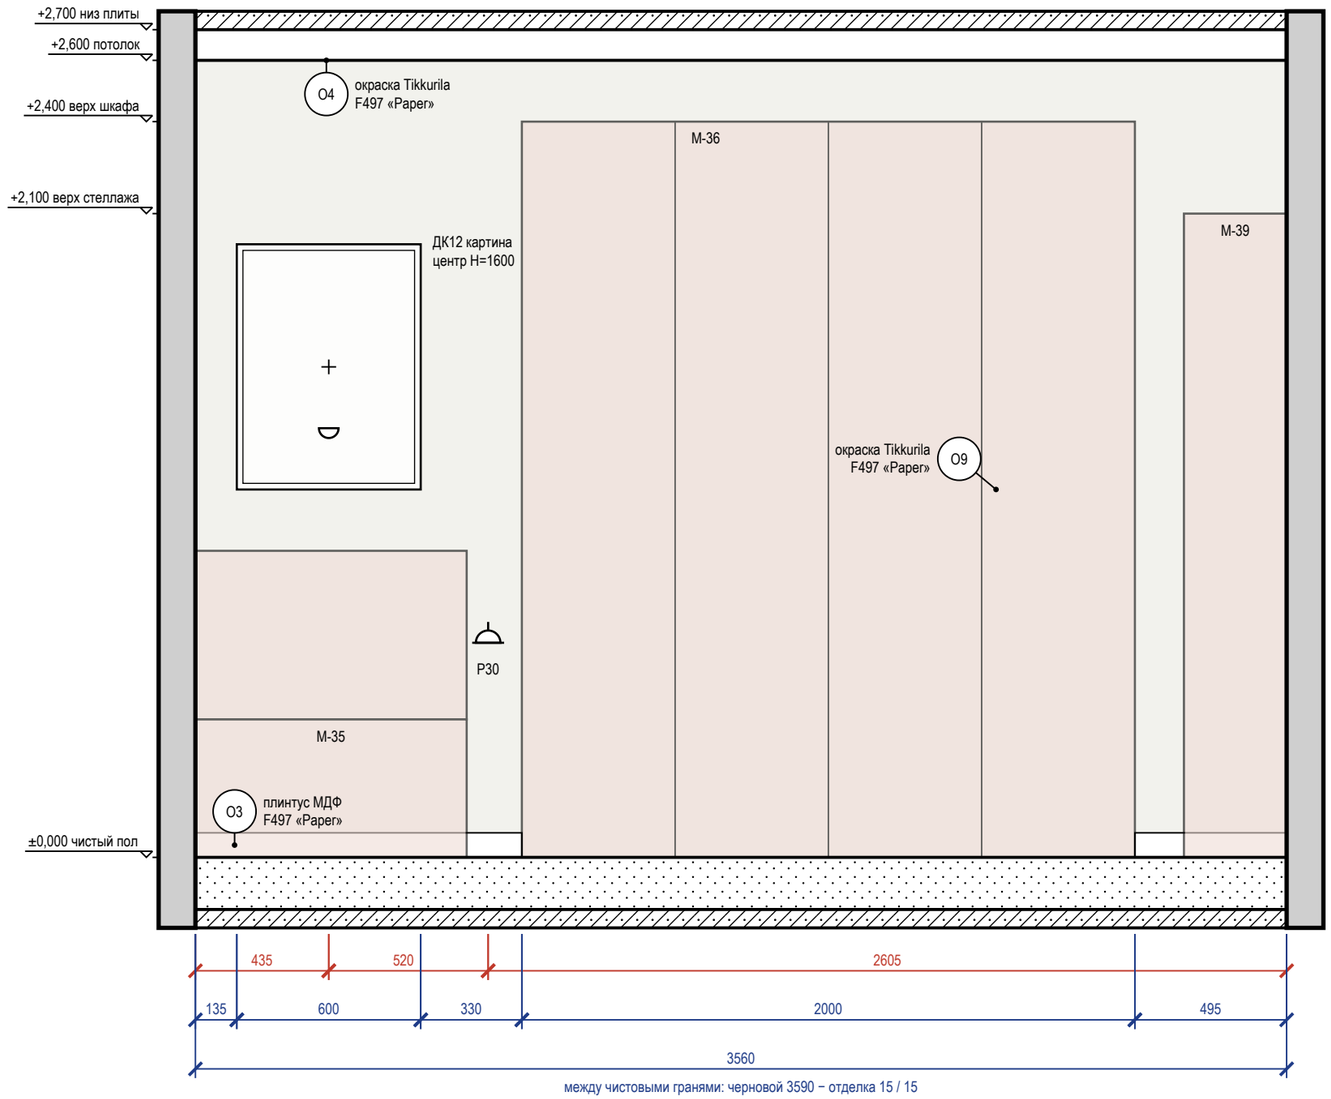


Стена А — визуализация, лист 15



Ведомость отделки (на листе)

Марка	Поверхность	Материал, изделие	Цвет, код	Кол.
О3	плинтус	плинтус МДФ, h 80 мм, аналог: плинтус МДФ под окраску 80×16 мм, полуглянцевая	Tikkurila F497 «Paper»	1,6 м
О4	потолок	окраска, Tikkurila Anti-Reflex 2, глубокоматовая, подготовка Q3	Tikkurila F497 «Paper»	11 м²
О9	стены	окраска, Tikkurila Joker, шелковисто-матовая, подготовка К3	Tikkurila F497 «Paper»	9,3 м²

Схема развёрток (М 1:50)

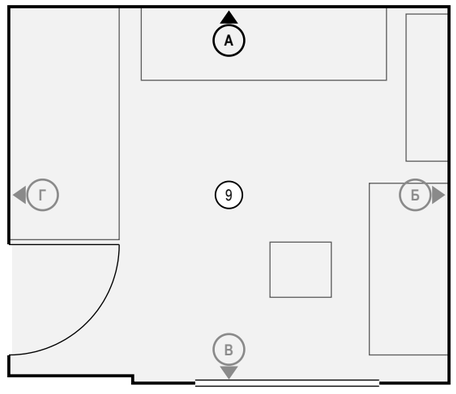

Ведомость точек и выводов

Марка	Что это	Гр.	Н, мм	От угла, мм	Примечание
Св63	светильник настенный	3	1400	435	
Р30	розетка: у кровати М-35	7	700	955	

Ведомость изделий и проёмов (на листе)

Марка	Изделие, проём	На виде Ш×В, мм	Низ, мм
М-35	кровать 900×1900	885×450	0
ДК12	картина	600×800	1200
М-36	шкаф распашной, 4 секции	2000×2400	0
М-39	стеллаж книжный	335×2100	0

Примечания

1. Размеры — в мм от чистовых поверхностей стен; условные обозначения и общие указания — лист 19.
2. Картины и зеркала крепить к основанию по паспорту изделия (закладные и анкеры — в перечне скрытых работ); крест — ось центра предмета.
3. Часть марок не уместилась у знаков: коды, высоты и привязки этих позиций — в ведомости точек и выводов под видами.

	Лист	№ док.	Подпись	Дата
Дизайнер	Кырлан А.С.			14.11.26
Проверил				
Н. контр.				
Утв.				


Проект: Четырёхкомнатная квартира — М 1:20

Развёртка стены А. Детская 2 (пом. 9)

Стадия	Лист	Листов
П	94	147

выпуск 14.11.2026 № e7147312ff · стр. 94 из 147

Стена Б (М 1:20)

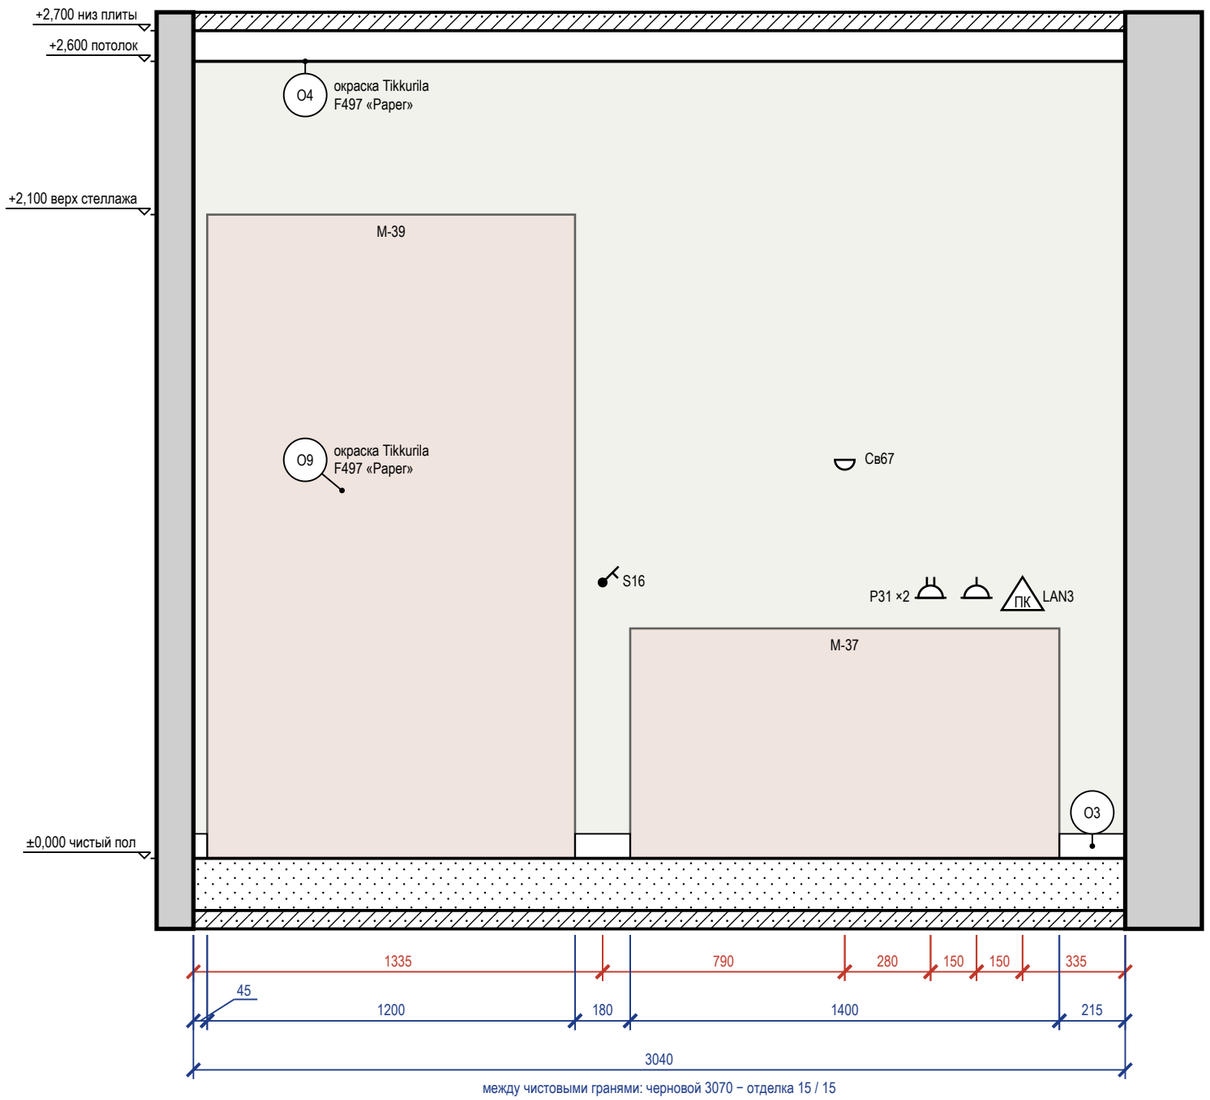

Ведомость точек и выводов

Марка	Что это	Гр.	Н, мм	От угла, мм	Примечание
S16	выключатель	3	900	1335	
Св67	светильник настенный	3	1300	2125	
Р31	розетка: рабочий стол М-37	7	850	2405	рамка 2 поста
Р32	розетка: рабочий стол М-37	7	850	2555	
LAN3	розетка RJ45: рабочий стол М-37		850	2705	


Ведомость изделий и проёмов (на листе)

Марка	Изделие, проём	На виде Ш×В, мм	Низ, мм
М-39	стеллаж книжный	1200×2100	0
М-37	стол письменный у стены Б, рядом с окном стены В: свет боковой	1400×750	0

Ведомость отделки (на листе)

Марка	Поверхность	Материал, изделие	Цвет, код	Кол.
О3	плинтус	плинтус МДФ, h 80 мм, аналог: плинтус МДФ под окраску 80×16 мм, полуглянцевая	Tikkurila F497 «Paper»	0,4 м
О4	потолок	окраска, Tikkurila Anti-Reflex 2, глубокоматовая, подготовка Q3	Tikkurila F497 «Paper»	11 м²
О9	стены	окраска, Tikkurila Joker, шелковисто-матовая, подготовка К3	Tikkurila F497 «Paper»	7,9 м²

Схема развёрток (М 1:50)

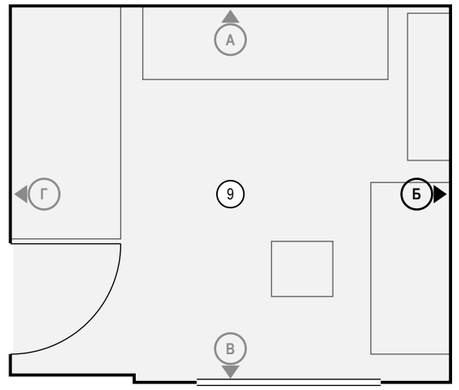


Примечания

1. Размеры — в мм от чистовых поверхностей стен; условные обозначения и общие указания — лист 19.
2. Часть марок не уместилась у знаков: коды, высоты и привязки этих позиций — в ведомости точек и выводов под видами.

	Лист	№ док.	Подпись	Дата	Проект: Четырёхкомнатная квартира			М 1:20
Дизайнер	Кырлан А.С.			14.11.26	Развёртка стены Б. Детская 2 (пом. 9)	Стадия	Лист	Листов
Проверил						П	95	147
Н. контр.								
Утв.								

выпуск 14.11.2026 № e7147312ff · стр. 95 из 147

Стена В (М 1:20)

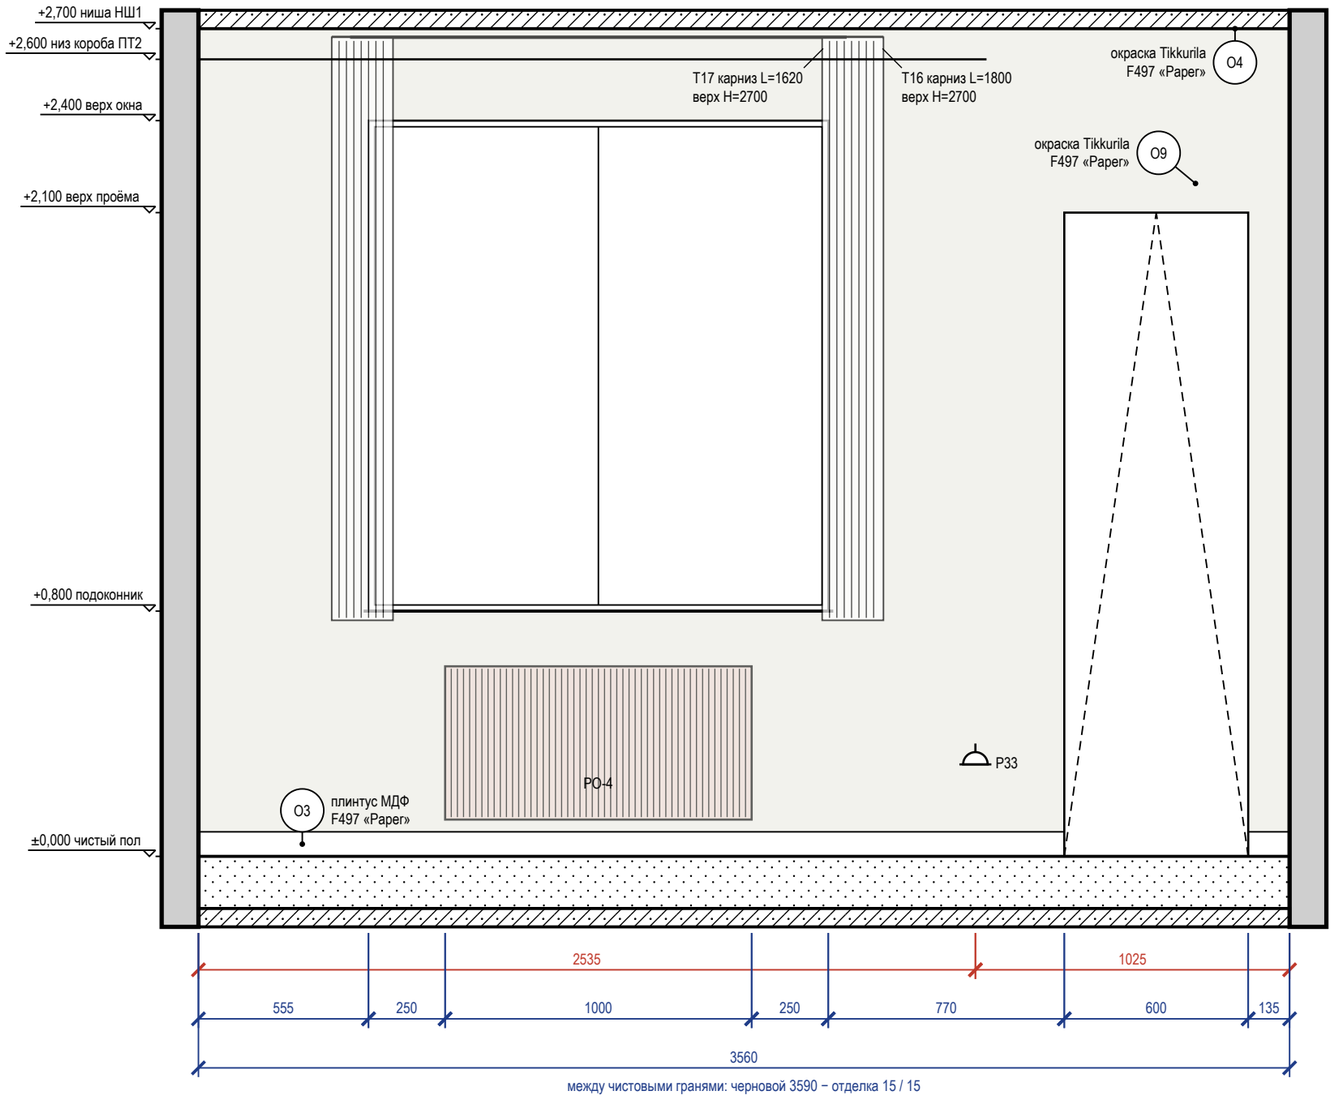

Ведомость точек и выводов

Марка	Что это	Гр.	H, мм	От угла, мм	Примечание
Р33	розетка: уборка	7	300	2535	


Ведомость изделий и проёмов (на листе)

Марка	Изделие, проём	На виде Ш×В, мм	Низ, мм
РО-4	радиатор отопления	1000×500	120

Ведомость отделки (на листе)

Марка	Поверхность	Материал, изделие	Цвет, код	Кол.
О3	плинтус	плинтус МДФ, h 80 мм, аналог: плинтус МДФ под окраску 80×16 мм, полуглянцевая	Tikkurila F497 «Paper»	3 м
О4	потолок	окраска, Tikkurila Anti-Reflex 2, глубокоматовая, подготовка Q3	Tikkurila F497 «Paper»	11 м²
О9	стены	окраска, Tikkurila Joker, шелковисто-матовая, подготовка К3	Tikkurila F497 «Paper»	6 м²

Схема развёрток (М 1:50)

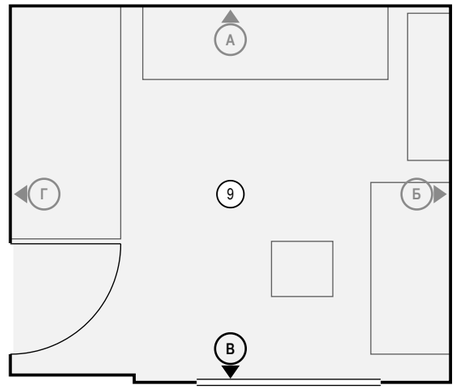

Примечания

1. Размеры — в мм от чистовых поверхностей стен; условные обозначения и общие указания — лист 19.
2. Карнизы (шины) — по ведомости текстиля декоратора: длина L и верх H на развёртке — те же числа, что в ведомости; крепление — до окраски потолка.

	Лист	№ док.	Подпись	Дата
Дизайнер	Кырлан А.С.			14.11.26
Проверил				
Н. контр.				
Утв.				


Проект: Четырёхкомнатная квартира — М 1:20

Развёртка стены В. Детская 2 (пом. 9)

Стадия	Лист	Листов
П	96	147

выпуск 14.11.2026 № e7147312ff · стр. 96 из 147

Стена Г (М 1:20)

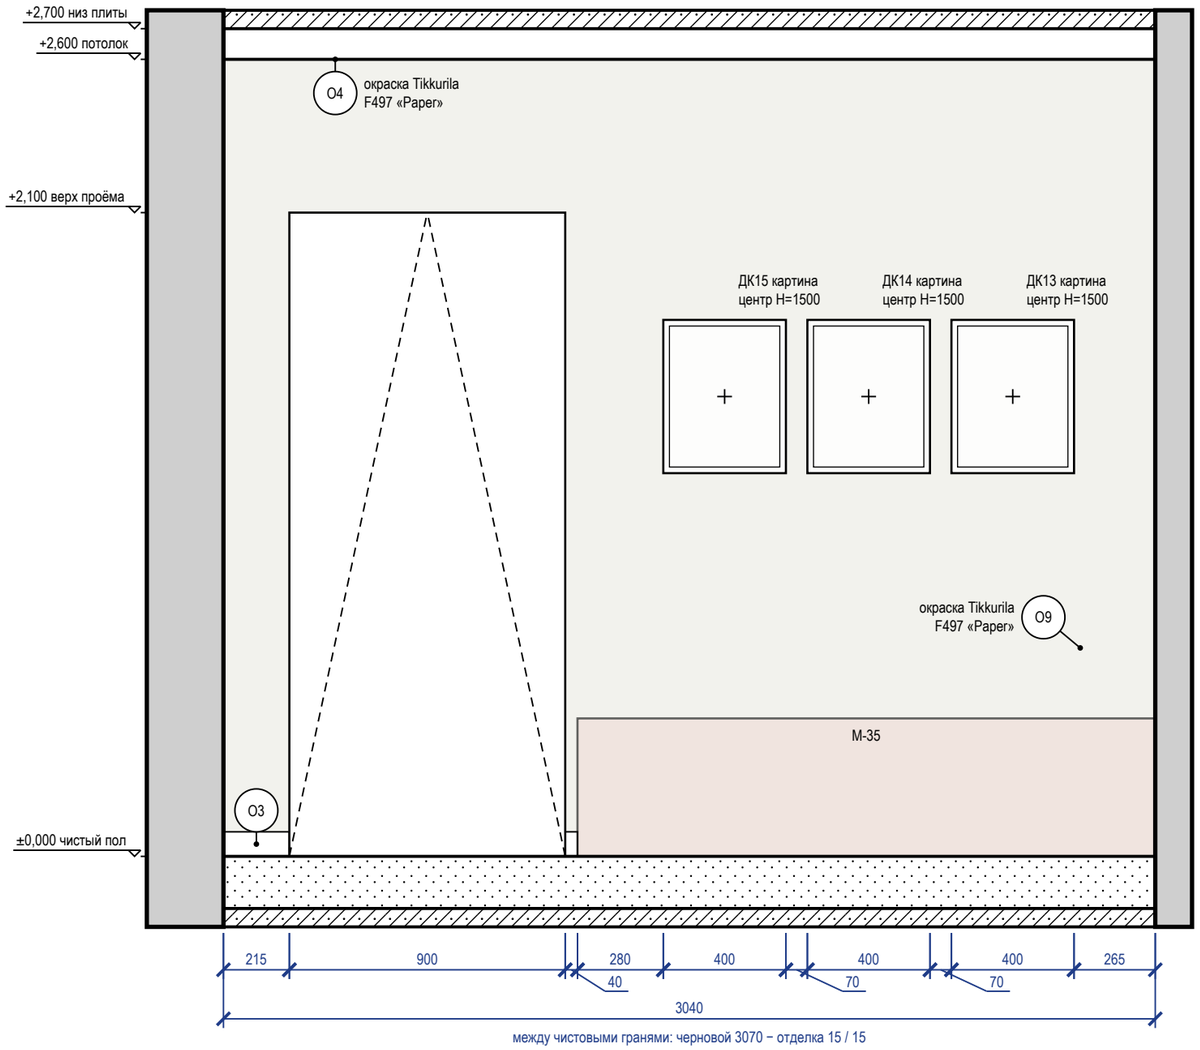


Ведомость изделий и проёмов (на листе)

Марка	Изделие, проём	На виде Ш×В, мм	Низ, мм
М-35	кровать 900×1900	1885×450	0
ДК15	картина	400×500	1250
ДК14	картина	400×500	1250
ДК13	картина	400×500	1250

Ведомость отделки (на листе)


Марка	Поверхность	Материал, изделие	Цвет, код	Кол.
О3	плинтус	плинтус МДФ, h 80 мм, аналог: плинтус МДФ под окраску 80×16 мм, полуглянцевая	Tikkurila F497 «Paper»	0,3 м
О4	потолок	окраска, Tikkurila Anti-Reflex 2, глубокоматовая, подготовка Q3	Tikkurila F497 «Paper»	11 м²
О9	стены	окраска, Tikkurila Joker, шелковисто-матовая, подготовка К3	Tikkurila F497 «Paper»	6 м²

Схема развёрток (М 1:50)

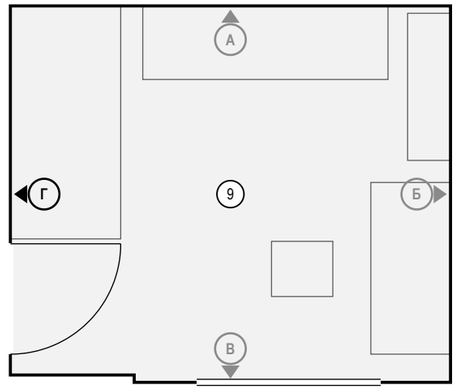

5 **Плинтус МДФ 80×16 мм у окрашенной стены по доске (ламинату) (М 1:10)**

Узел 5 — лист С14

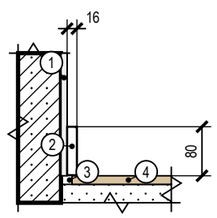

Поз.	Состав слоя, изделие
1	штукатурка, шпаклёвка Q3, окраска — по ведомости отделки
2	плинтус МДФ 80×16 под окраску в цвет стены; клей монтажный — к стене, не к полу
3	зазор покрытия у стены 8–10 мм закрывается плинтусом
4	инженерная доска дуб на клею


Примечания

1. Размеры — в мм от чистовых поверхностей стен; условные обозначения и общие указания — лист 19.
2. Картины и зеркала крепить к основанию по паспорту изделия (закладные и анкеры — в перечне скрытых работ); крест — ось центра предмета.

	Лист	№ док.	Подпись	Дата	Проект: Четырёхкомнатная квартира			М 1:20
Дизайнер	Кырлан А.С.			14.11.26				
Проверил					Развёртка стены Г. Детская 2 (пом. 9)	Стадия	Лист	Листов
Н. контр.						П	97	147
Утв.								


выпуск 14.11.2026 № e7147312ff · стр. 97 из 147

Стена А (М 1:20)

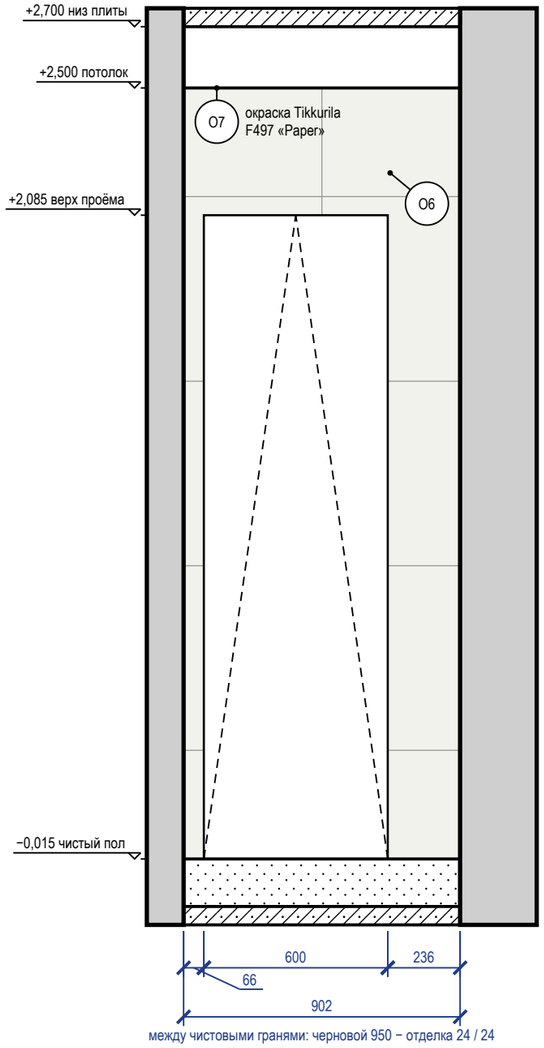

между чистовыми гранями: черновой 950 − отделка 24 / 24

Стена Б (М 1:20)

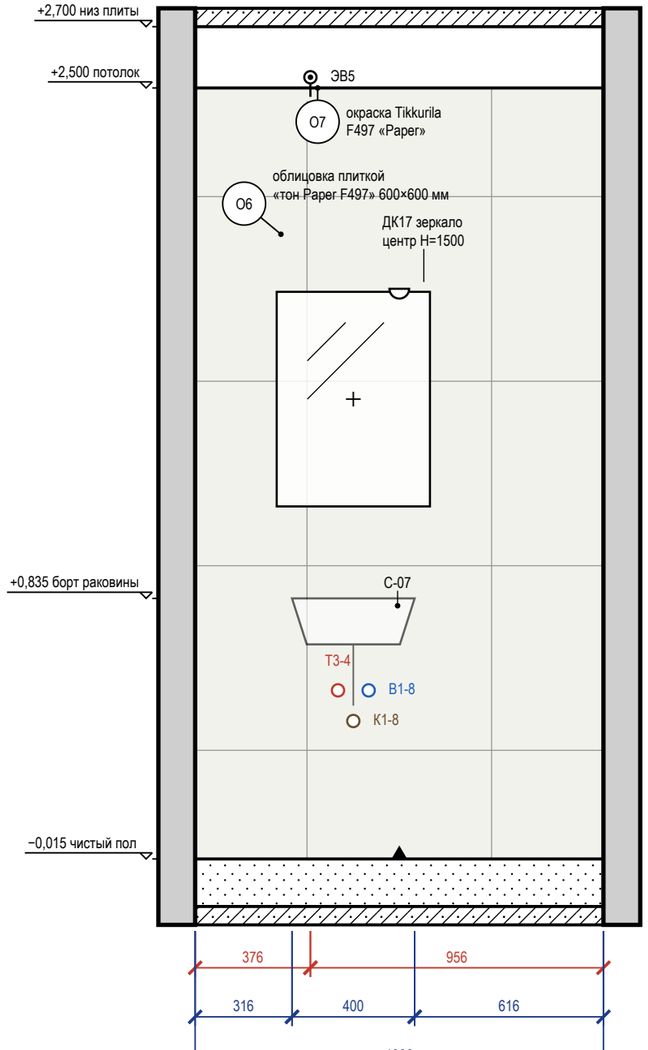


между чистовыми гранями: черновой 1380 − отделка 24 / 24

Ведомость отделки (на листе)

Марка	Поверхность	Материал, изделие	Цвет, код	Кол.
О6	стены	облицовка плиткой, 600×600×9 мм, аналог: керамогранит матовый, тон F497, затирка CG2WA	#F1F1EC «тон Paper F497»	4,4 м²
О7	потолок	окраска, Tikkurila Luja 7, матовая, подготовка Q3	Tikkurila F497 «Paper»	1,3 м²

Схема развёрток (М 1:50)

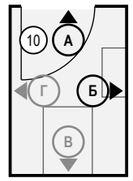

Ведомость точек и выводов

Стена	Марка	Что это	Гр.	H, мм	От угла, мм	Примечание
Б	ЭВ5	вывод кабеля: вентилятор ВР3 (таймер выбега)	4	2550	376	
Б	Т3-4	горячая вода — умывальник		550	466	межос. 100
Б	К1-8	канализация — умывальник		450	516	Ø40

Стена	Марка	Что это	Гр.	H, мм	От угла, мм	Примечание
Б	В1-8	холодная вода — умывальник		550	566	межос. 100
Б	Св64	светильник настенный	4	1860	666	

Ведомость изделий и проёмов (на листе)


Стена	Марка	Изделие, проём	На виде Ш×В, мм	Низ, мм
Б	ДК17	зеркало	500×700	1150
Б	С-07	раковина подвесная компактная 400×220	400×150	700

Примечания


1. Размеры — в мм от чистовых поверхностей стен; условные обозначения и общие указания — лист 19.
2. Облицовка — по сетке швов 2 мм, раскладка от оси стены (треугольник у пола), по высоте — от середины облицовки, подрезки у пола и у потолка поровну; подрезки — по листу раскладки плитки.
3. Гидроизоляция в 2 слоя, заход на стены 200 мм — до облицовки, с актом скрытых работ и тестом проливом (узел — на листе узлов).
4. Картины и зеркала крепить к основанию по паспорту изделия (закладные и анкеры — в перечне скрытых работ); крест — ось центра предмета.
5. Линии узора (швы плитки, складки штор, рёбра радиаторов) прерываются у знаков и выносок — просвет между линиями не менее 0,7 мм.
6. Часть марок не уместилась у знаков: коды, высоты и привязки этих позиций — в ведомости точек и выводов под видами.

	Лист	№ док.	Подпись	Дата	Проект: Четырёхкомнатная квартира	М 1:20
Дизайнер	Кырлан А.С.			14.11.26		
Проверил					Развёртки стен А, Б. Санузел (пом. 10)	Стадия: П; Лист: 98; Листов: 147
Н. контр.						
Утв.						

Стена В (М 1:20)

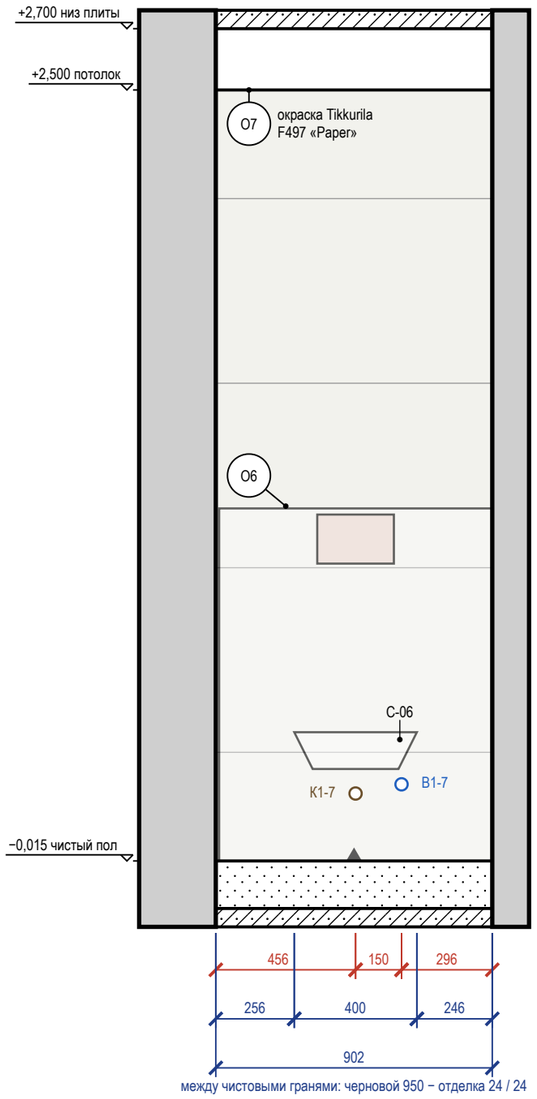


Стена Г (М 1:20)

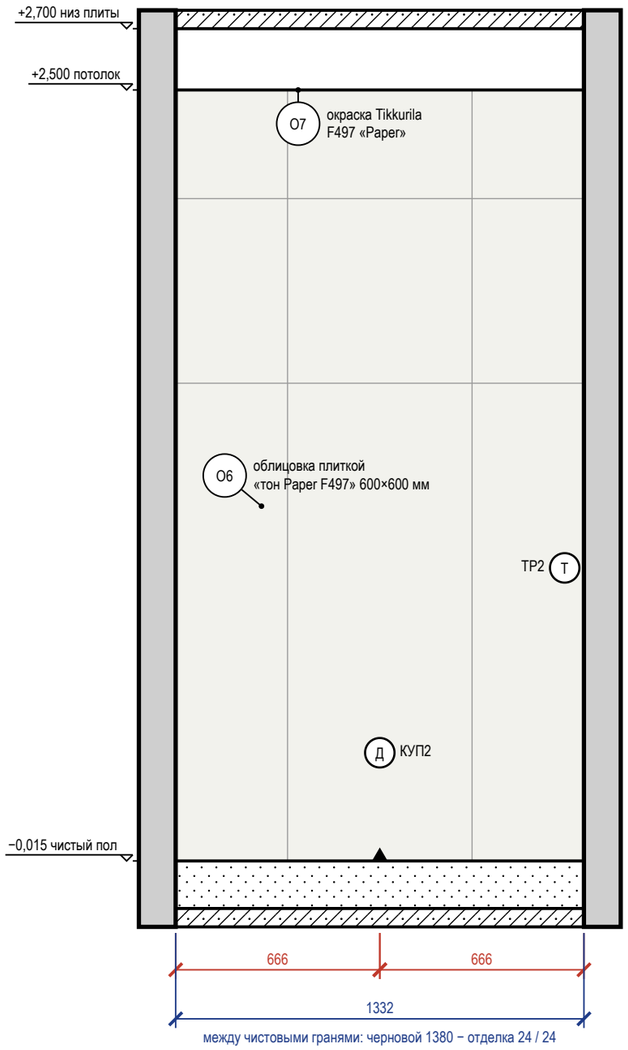

Ведомость точек и выводов

Стена	Марка	Что это	Гр.	Н, мм	От угла, мм	Примечание
В	К1-7	канализация — унитаз подвесной		220	456	Ø110
В	В1-7	холодная вода — унитаз подвесной		250	606	в раме инсталляции
Г	КУП2	КУП (уравнивание потенциалов): КУП коробка уравнивания потенциалов (ДСУП)		353	666	
Г	ТР2	терморегулятор: терморегулятор тёплого пола санузла	17	956	1269	


Стена В — визуализация, лист 16

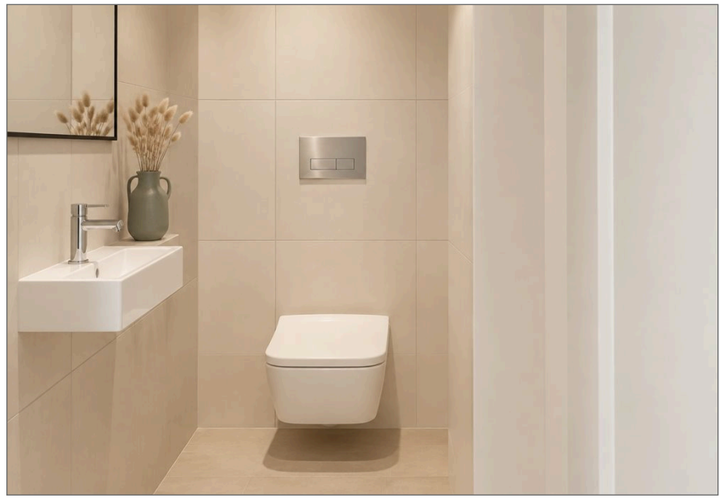

Ведомость отделки (на листе)

Марка	Поверхность	Материал, изделие	Цвет, код	Кол.
О6	стены	облицовка плиткой, 600×600×9 мм, аналог: керамогранит матовый, тон F497, затирка CG2WA	#F1F1EC «тон Paper F497»	5,6 м²
О7	потолок	окраска, Tikkurila Luja 7, матовая, подготовка Q3	Tikkurila F497 «Paper»	1,3 м²

Схема развёрток (М 1:50)

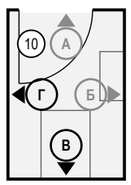

Ведомость изделий и проёмов (на листе)

Стена	Марка	Изделие, проём	На виде Ш×В, мм	Низ, мм
В	С-06	унитаз подвесной с инсталляцией	400×120	300


Примечания

1. Размеры — в мм от чистовых поверхностей стен; условные обозначения и общие указания — лист 19.
2. Облицовка — по сетке швов 2 мм, раскладка от оси стены (треугольник у пола), по высоте — от середины облицовки, подрезки у пола и у потолка поровну; подрезки — по листу раскладки плитки.
3. Гидроизоляция в 2 слоя, заход на стены 200 мм — до облицовки, с актом скрытых работ и тестом проливом (узел — на листе узлов).

	Лист	№ док.	Подпись	Дата	Проект: Четырёхкомнатная квартира			М 1:20
Дизайнер	Кырлан А.С.			14.11.26	Развёртки стен В, Г. Санузел (пом. 10)	Стадия	Лист	Листов
Проверил						П	99	147
Н. контр.								
Утв.								

выпуск 14.11.2026 № e7147312ff · стр. 99 из 147

Стена А (М 1:20)

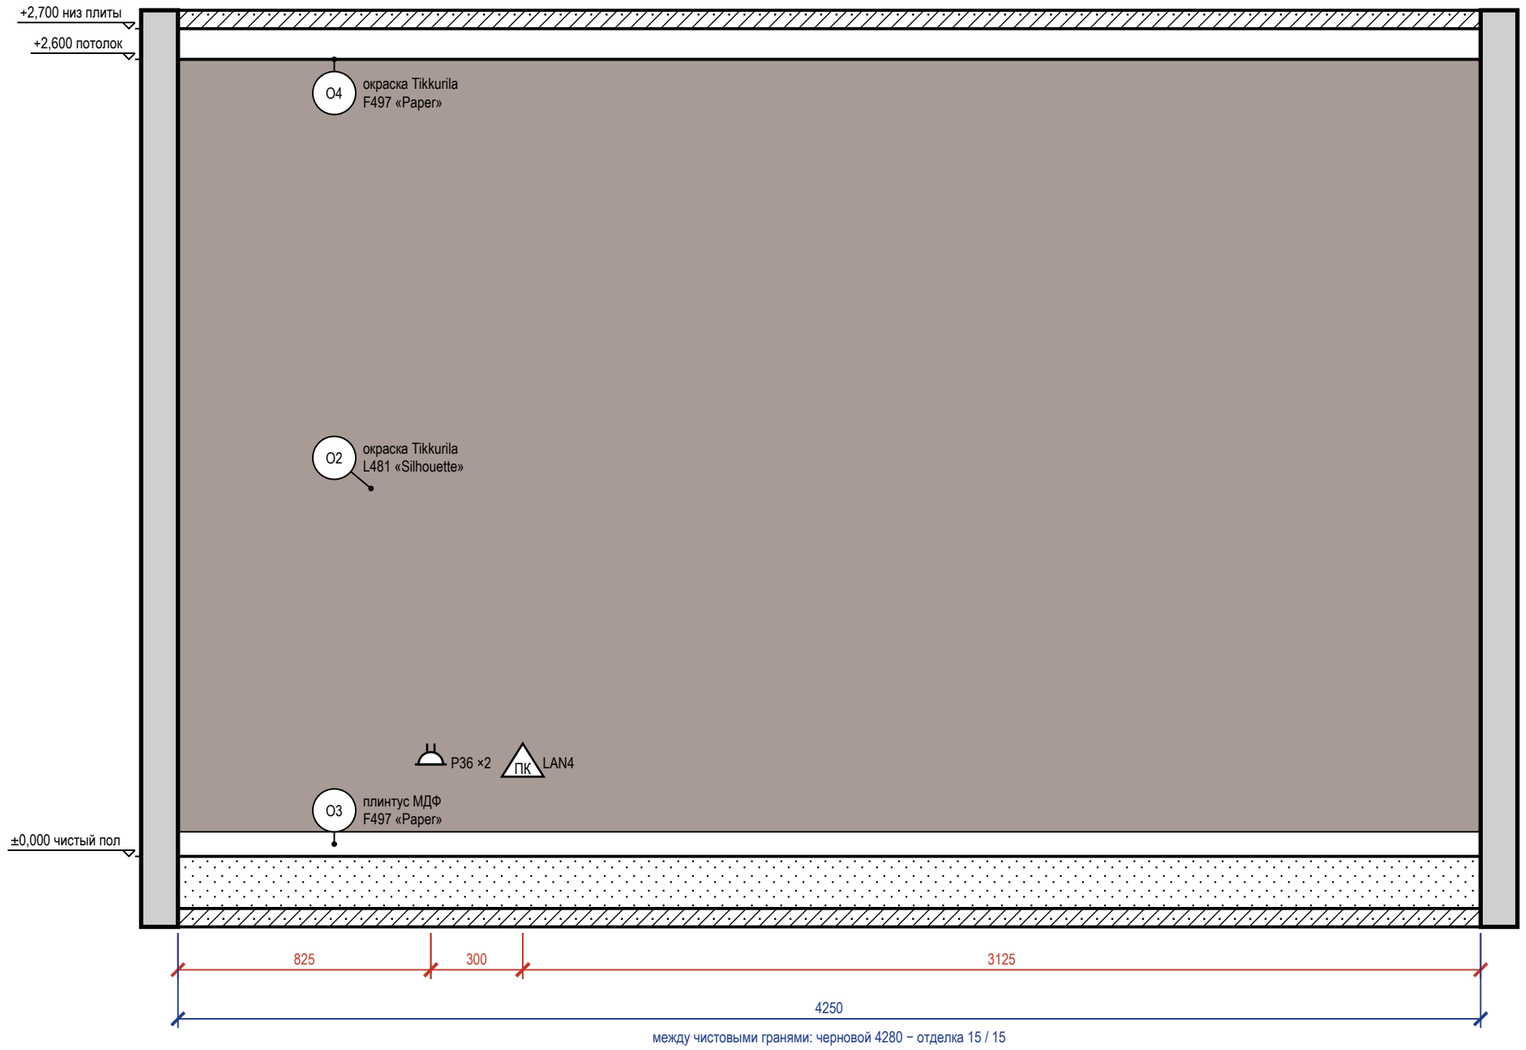

Ведомость точек и выводов

Марка	Что это	Гр.	Н, мм	От угла, мм	Примечание
Р36	розетка	19	300	825	рамка 2 поста
LAN4	розетка RJ45		300	1125	

Стена А — визуализация, лист 17


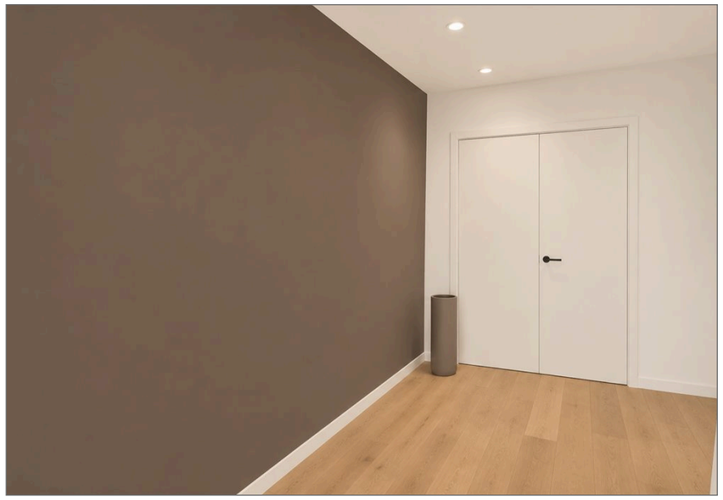


Схема развёрток (М 1:50)

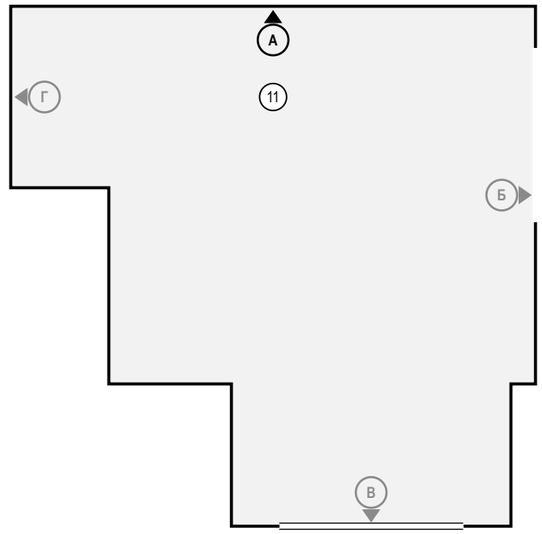

Ведомость отделки (на листе)

Марка	Поверхность	Материал, изделие	Цвет, код	Кол.
О2	акцентная стена	окраска, Tikkurila Optiva 5 Matt, аналог: интерьерная краска, класс 2 по EN 13300, глубокоматовая/матовая, база С, матовая, подготовка К3	Tikkurila L481 «Silhouette»	11,1 м²
О3	плинтус	плинтус МДФ, h 80 мм, аналог: плинтус МДФ под окраску 80×16 мм, полуглянцевая	Tikkurila F497 «Paper»	4,3 м
О4	потолок	окраска, Tikkurila Anti-Reflex 2, глубокоматовая, подготовка Q3	Tikkurila F497 «Paper»	14,6 м²

Примечания

1. Размеры — в мм от чистовых поверхностей стен; условные обозначения и общие указания — лист 19.

	Лист	№ док.	Подпись	Дата
Дизайнер	Кырлан А.С.			14.11.26
Проверил				
Н. контр.				
Утв.				


Проект: Четырёхкомнатная квартира — **М 1:20**

Развёртка стены А. Гостиная (пом. 11)

Стадия	Лист	Листов
П	100	147

выпуск 14.11.2026 № e7147312ff · стр. 100 из 147

Стена Б (М 1:20)

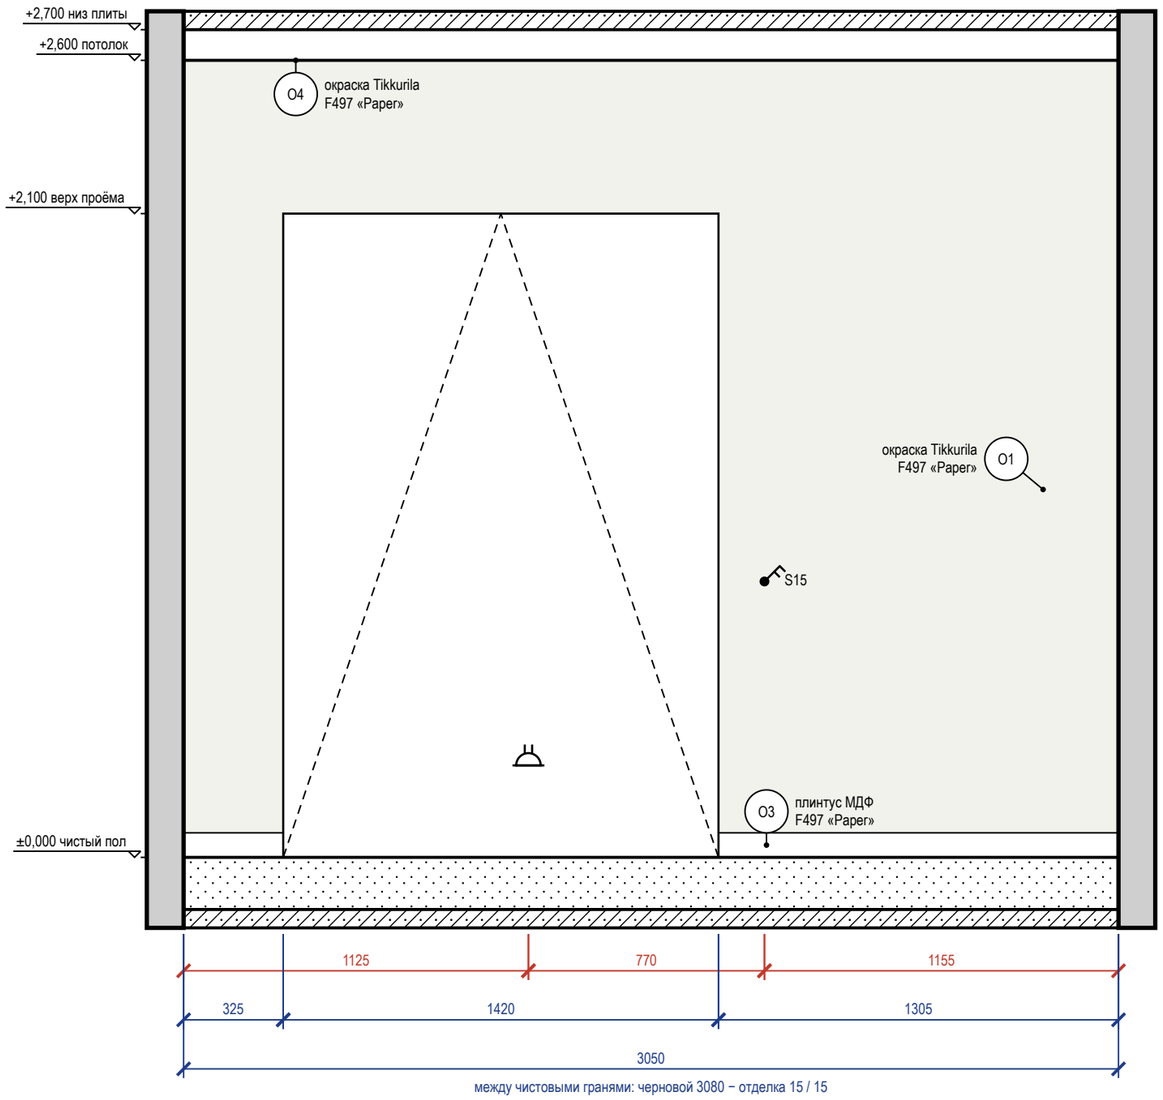


Ведомость точек и выводов

Марка	Что это	Гр.	Н, мм	От угла, мм	Примечание
P38	розетка	19	300	1125	рамка 2 поста
S15	выключатель	3	900	1895	

Ведомость отделки (на листе)

Марка	Поверхность	Материал, изделие	Цвет, код	Кол.
O1	стены	окраска, Tikkurila Optiva 5 Matt, матовая, подготовка К3	Tikkurila F497 «Paper»	4,9 м²
O3	плинтус	плинтус МДФ, h 80 мм, аналог: плинтус МДФ под окраску 80×16 мм, полуглянцевая	Tikkurila F497 «Paper»	1,6 м
O4	потолок	окраска, Tikkurila Anti-Reflex 2, глубокоматовая, подготовка Q3	Tikkurila F497 «Paper»	14,6 м²

Схема развёрток (М 1:50)

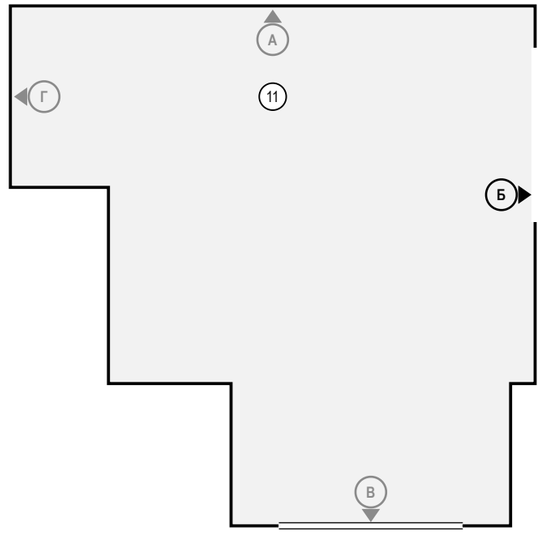


Примечания

1. Размеры — в мм от чистовых поверхностей стен; условные обозначения и общие указания — лист 19.
2. Часть марок не уместилась у знаков: коды, высоты и привязки этих позиций — в ведомости точек и выводов под видами.

	Лист	№ док.	Подпись	Дата	Проект: Четырёхкомнатная квартира			М 1:20
Дизайнер	Кырлан А.С.			14.11.26	Развёртка стены Б. Гостиная (пом. 11)	Стадия	Лист	Листов
Проверил						П	101	147
Н. контр.								
Утв.								

выпуск 14.11.2026 № e7147312ff · стр. 101 из 147

Стена В (М 1:20)

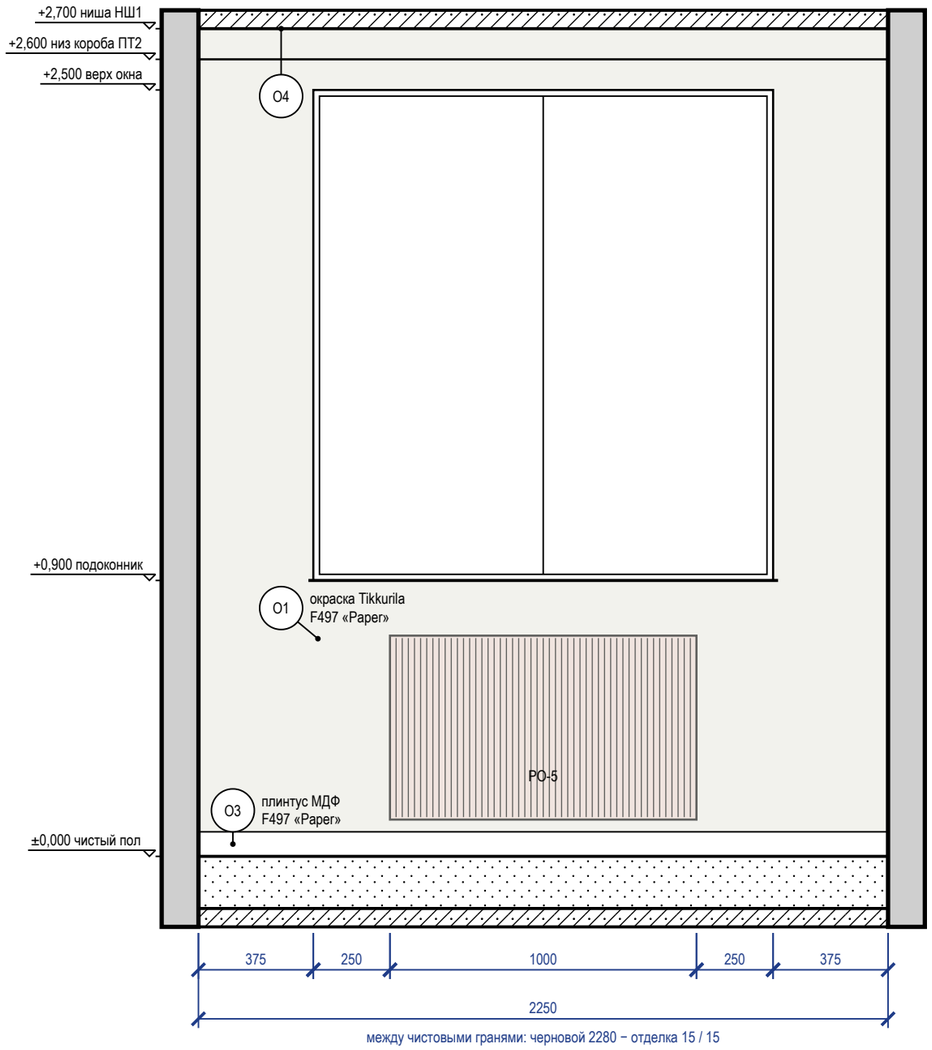

Стена Г (М 1:20)


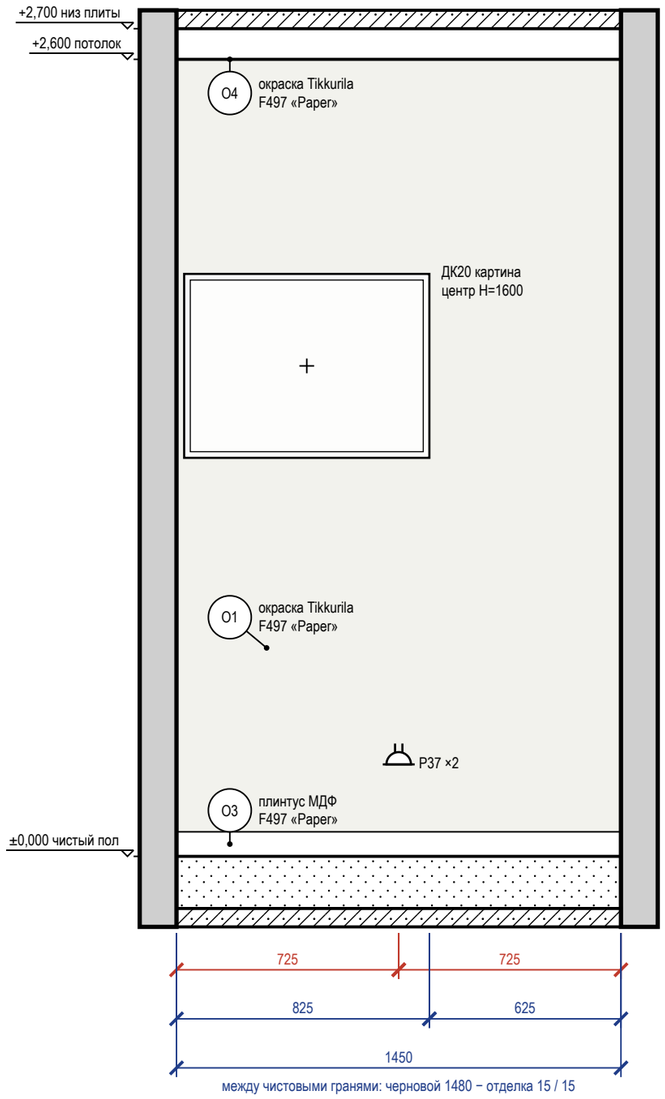


Схема развёрток (М 1:50)

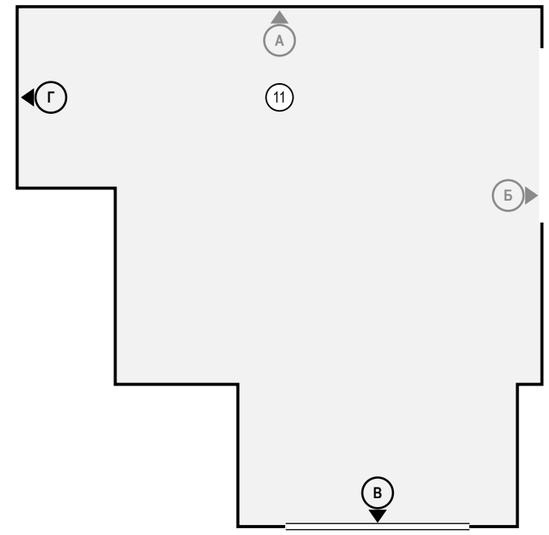

Ведомость точек и выводов

Стена	Марка	Что это	Гр.	H, мм	От угла, мм	Примечание
Г	Р37	розетка	19	300	725	рамка 2 поста

Ведомость изделий и проёмов (на листе)

Стена	Марка	Изделие, проём	На виде Ш×В, мм	Низ, мм
В	РО-5	радиатор отопления	1000×600	120
Г	ДК20	картина	800×600	1300

Ведомость отделки (на листе)

Марка	Поверхность	Материал, изделие	Цвет, код	Кол.
О1	стены	окраска, Tikkurila Optiva 5 Matt, матовая, подготовка К3	Tikkurila F497 «Paper»	7,4 м²
О3	плинтус	плинтус МДФ, h 80 мм, аналог: плинтус МДФ под окраску 80×16 мм, полуглянцевая	Tikkurila F497 «Paper»	3,7 м
О4	потолок	окраска, Tikkurila Anti-Reflex 2, глубокоматовая, подготовка Q3	Tikkurila F497 «Paper»	14,6 м²

Примечания

1. Размеры — в мм от чистовых поверхностей стен; условные обозначения и общие указания — лист 19.
2. Картины и зеркала крепить к основанию по паспорту изделия (закладные и анкеры — в перечне скрытых работ); крест — ось центра предмета.

	Лист	№ док.	Подпись	Дата
Дизайнер	Кырлан А.С.			14.11.26
Проверил				
Н. контр.				
Утв.				


Проект: Четырёхкомнатная квартира — **М 1:20**

Развёртки стен В, Г. Гостиная (пом. 11)


Стадия	Лист	Листов
П	102	147

выпуск 14.11.2026 № e7147312ff · стр. 102 из 147

Стена Б (М 1:20)

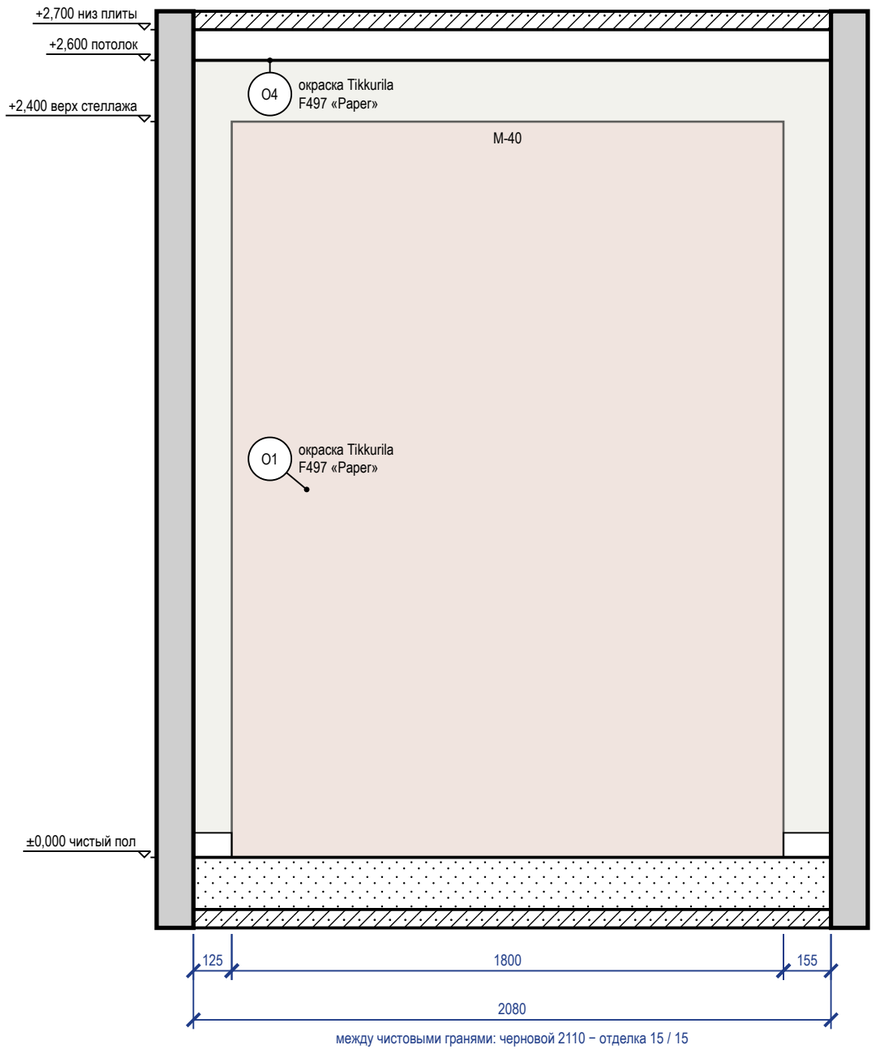

Стена В (М 1:20)

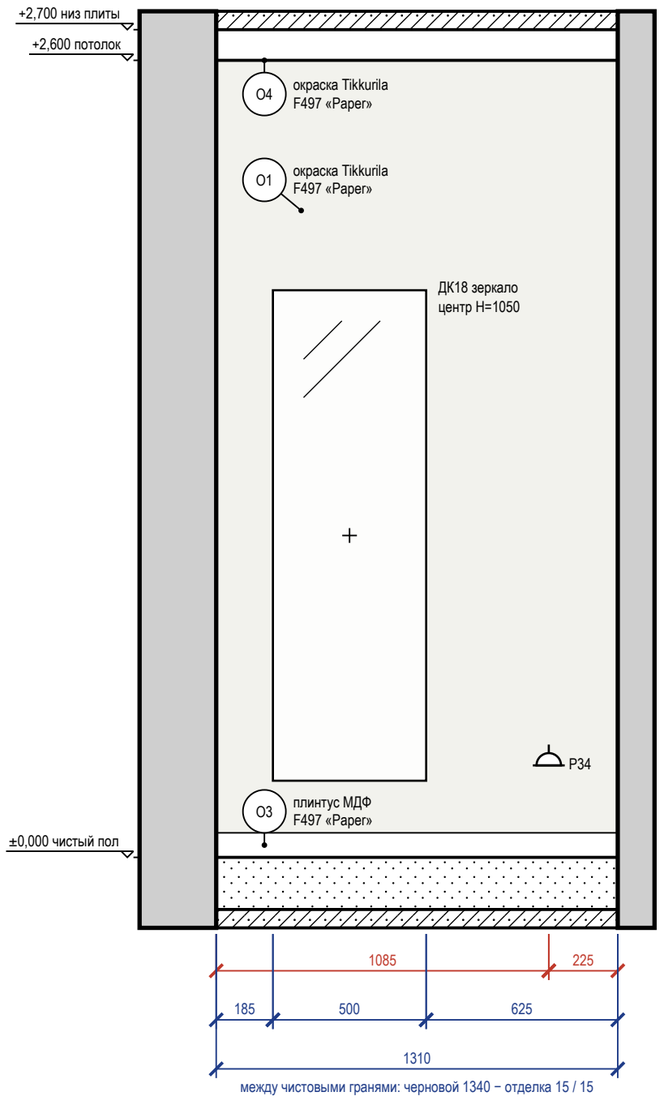


Стена Б — визуализация, лист 18



Ведомость отделки (на листе)

Марка	Поверхность	Материал, изделие	Цвет, код	Кол.
О1	стены	окраска, Tikkurila Optiva 5 Matt, матовая, подготовка К3	Tikkurila F497 «Paper»	8,8 м²
О3	плинтус	плинтус МДФ, h 80 мм, аналог: плинтус МДФ под окраску 80×16 мм, полуглянцевая	Tikkurila F497 «Paper»	1,6 м
О4	потолок	окраска, Tikkurila Anti-Reflex 2, глубокоматовая, подготовка Q3	Tikkurila F497 «Paper»	2,8 м²

Схема развёрток (М 1:50)

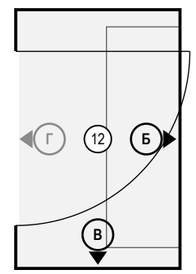

Ведомость точек и выводов

Стена	Марка	Что это	Гр.	Н, мм	От угла, мм	Примечание
В	Р34	розетка: уборка, отпариватель	8	300	1085	

Ведомость изделий и проёмов (на листе)

Стена	Марка	Изделие, проём	На виде Ш×В, мм	Низ, мм
Б	М-40	система хранения торцевая: штанги, полки	1800×2400	0
В	ДК18	зеркало	500×1600	250

Примечания

1. Размеры — в мм от чистовых поверхностей стен; условные обозначения и общие указания — лист 19.
2. Картины и зеркала крепить к основанию по паспорту изделия (закладные и анкеры — в перечне скрытых работ); крест — ось центра предмета.

	Лист	№ док.	Подпись	Дата
Дизайнер	Кырлан А.С.			14.11.26
Проверил				
Н. контр.				
Утв.				


Проект: Четырёхкомнатная квартира — **М 1:20**

Развёртки стен Б, В. Гардеробная 1 (пом. 12)

Стадия	Лист	Листов
П	103	147

выпуск 14.11.2026 № e7147312ff · стр. 103 из 147

Стена Г (М 1:20)

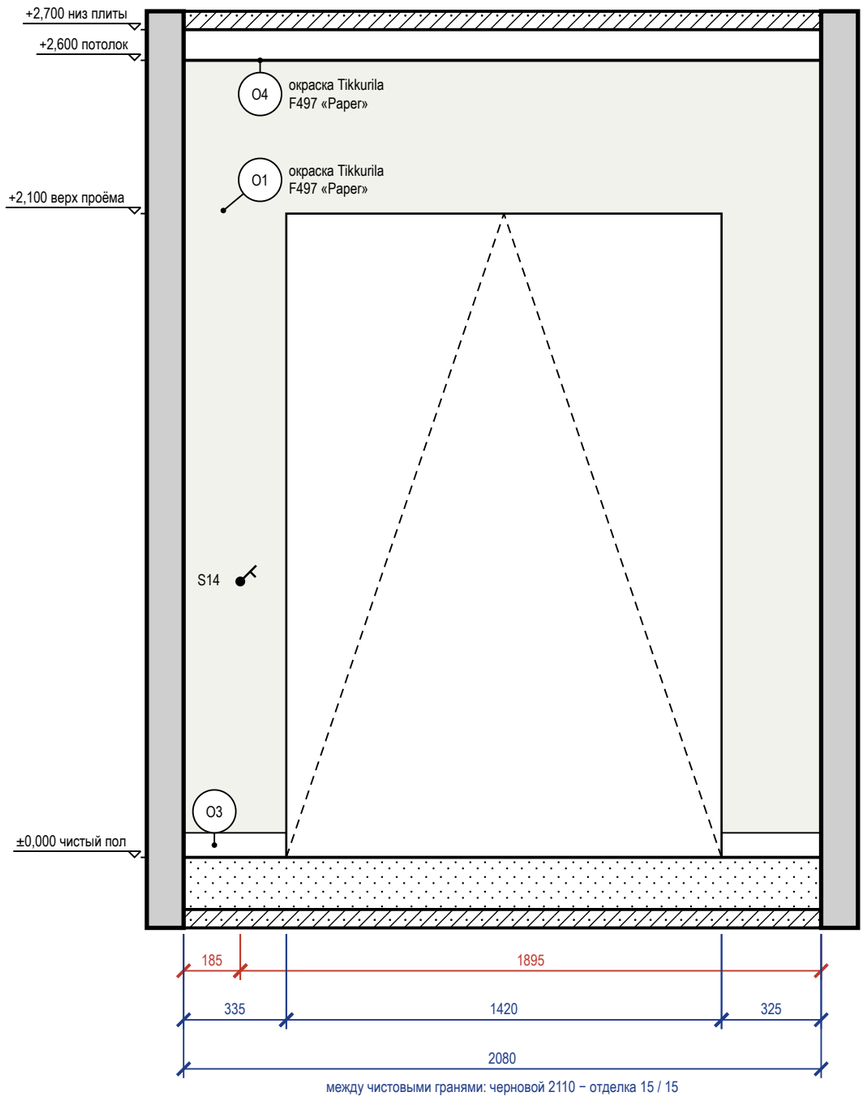


Ведомость точек и выводов

Марка	Что это	Гр.	Н, мм	От угла, мм	Примечание
S14	выключатель	2	900	185	

Ведомость отделки (на листе)

Марка	Поверхность	Материал, изделие	Цвет, код	Кол.
О1	стены	окраска, Tikkurila Optiva 5 Matt, матовая, подготовка К3	Tikkurila F497 «Paper»	2,4 м²
О3	плинтус	плинтус МДФ, h 80 мм, аналог: плинтус МДФ под окраску 80×16 мм, полуглянцевая	Tikkurila F497 «Paper»	0,7 м
О4	потолок	окраска, Tikkurila Anti-Reflex 2, глубокоматовая, подготовка Q3	Tikkurila F497 «Paper»	2,8 м²

Схема развёрток (М 1:50)

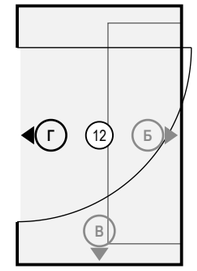


Примечания

1. Размеры — в мм от чистовых поверхностей стен; условные обозначения и общие указания — лист 19.


	Лист	№ док.	Подпись	Дата	Проект: Четырёхкомнатная квартира			М 1:20
Дизайнер	Кырлан А.С.			14.11.26	Развёртка стены Г. Гардеробная 1 (пом. 12)	Стадия	Лист	Листов
Проверил						П	104	147
Н. контр.								
Утв.								

выпуск 14.11.2026 № e7147312ff · стр. 104 из 147

Стена А (М 1:20)

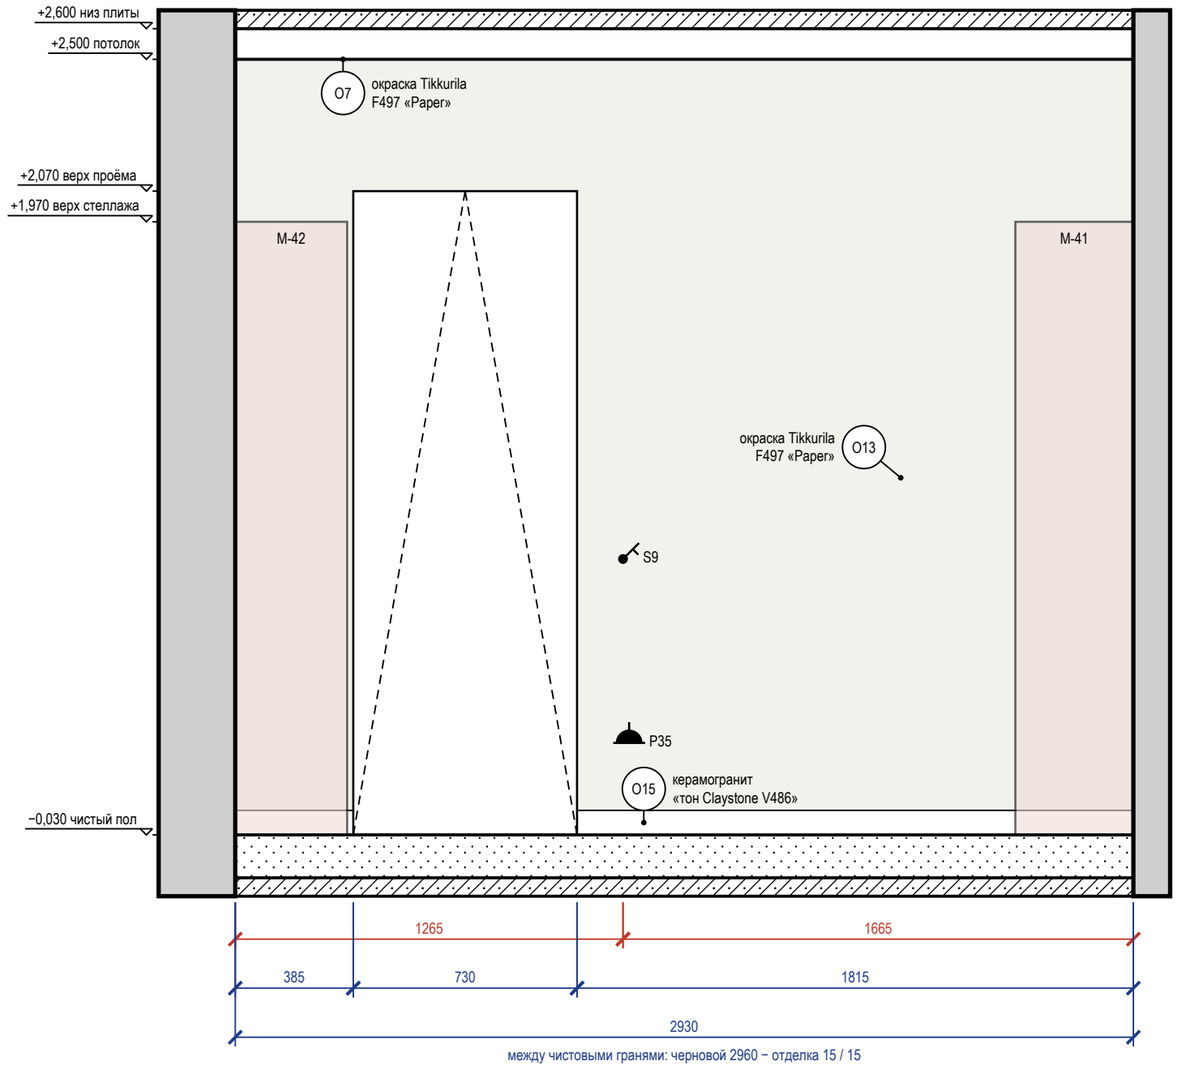

Стена Б (М 1:20)

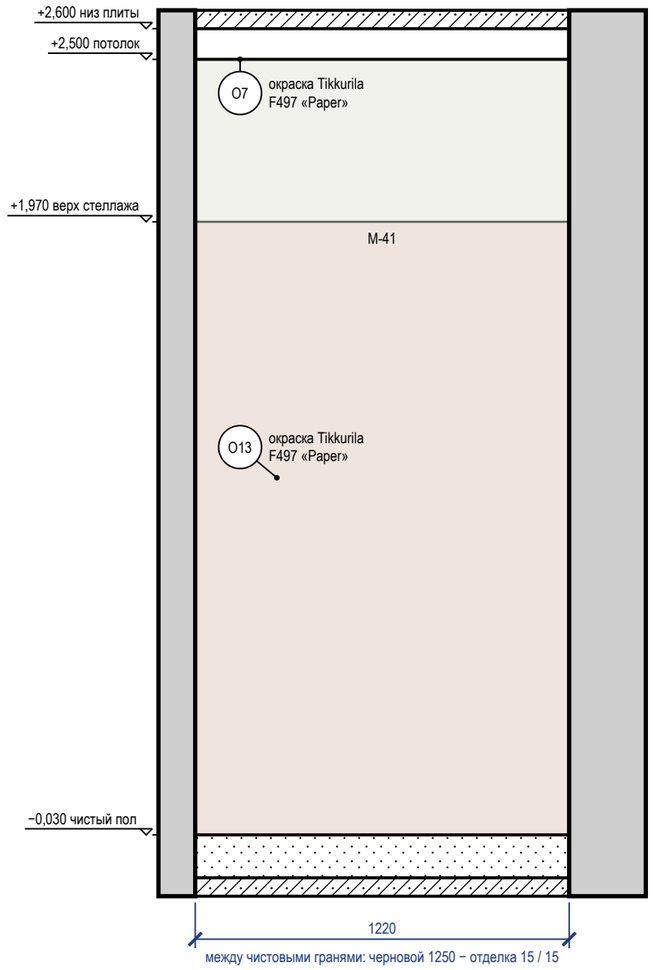


Ведомость точек и выводов

Стена	Марка	Что это	Гр.	H, мм	От угла, мм	Примечание
А	S9	выключатель	2	900	1265	
А	P35	розетка: балкон: розетка общего назначения	8	300	1285	IP44

Ведомость отделки (на листе)

Марка	Поверхность	Материал, изделие	Цвет, код	Кол.
О7	потолок	окраска, Tikkurila Luja 7, матовая, подготовка Q3	Tikkurila F497 «Paper»	3,7 м²
О13	стены	окраска, Tikkurila Luja 7, шелковисто-матовая, подготовка К3	Tikkurila F497 «Paper»	9 м²
О15	плинтус	керамогранит, аналог: плинтус из керамогранита пола, подрезка 80 мм, верхняя кромка с запилом 45°	#B8AFA5 «тон Claystone V486»	2,2 м

Схема развёрток (М 1:50)

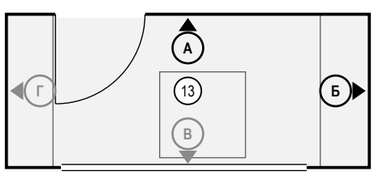


Примечания

1. Размеры — в мм от чистовых поверхностей стен; условные обозначения и общие указания — лист 19.


	Лист	№ док.	Подпись	Дата	Проект: Четырёхкомнатная квартира	М 1:20		
Дизайнер	Кырлан А.С.			14.11.26	Развёртки стен А, Б. Балкон 1 (пом. 13)	Стадия	Лист	Листов
Проверил						П	105	147
Н. контр.								
Утв.								

выпуск 14.11.2026 № e7147312ff · стр. 105 из 147

Стена В (М 1:20)

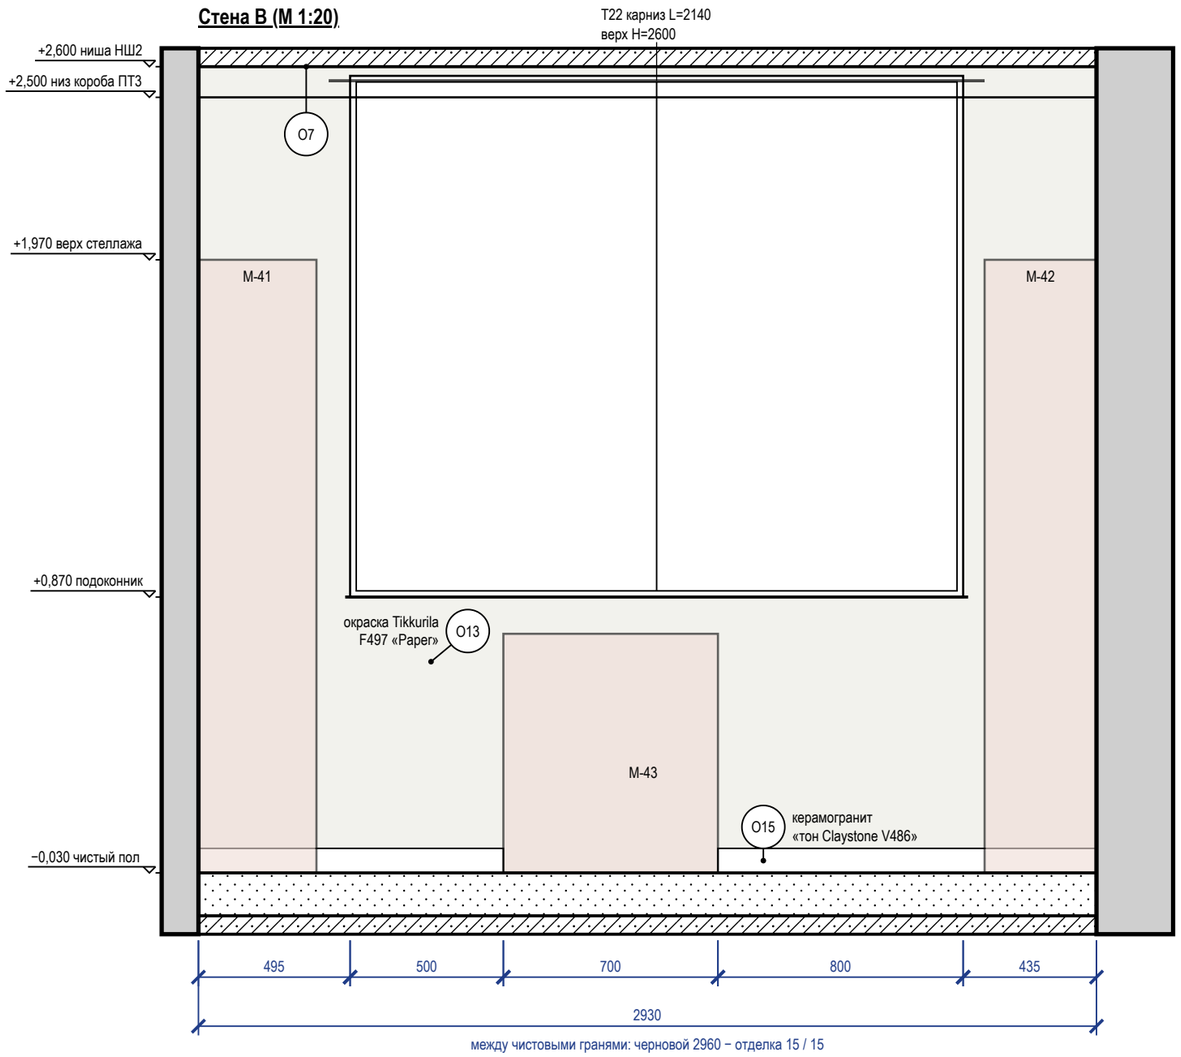


Стена Г (М 1:20)

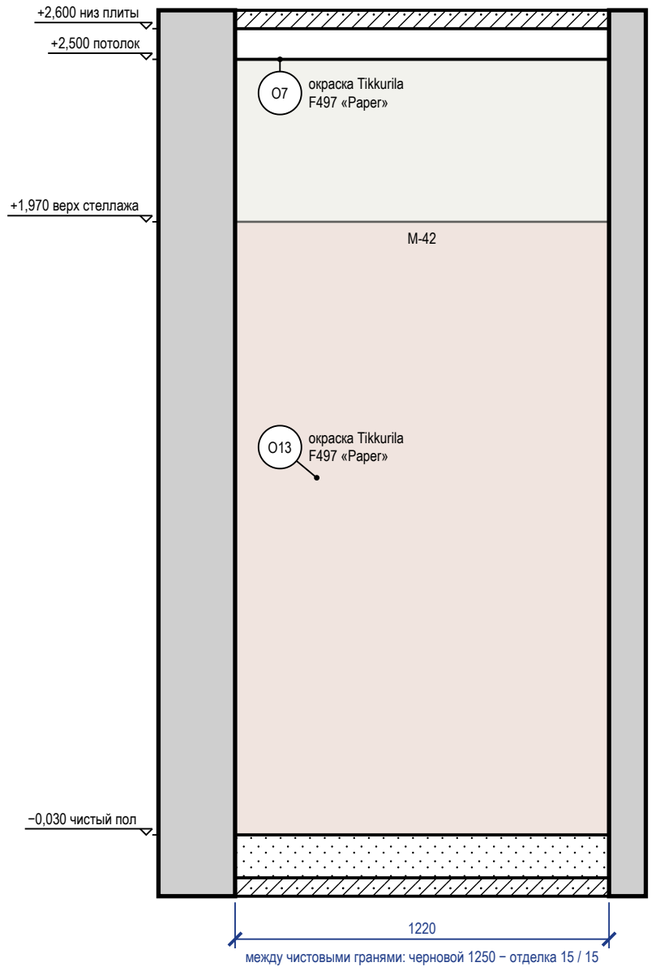

Ведомость отделки (на листе)

Марка	Поверхность	Материал, изделие	Цвет, код	Кол.
О7	потолок	окраска, Tikkurila Luja 7, матовая, подготовка Q3	Tikkurila F497 «Paper»	3,7 м²
О13	стены	окраска, Tikkurila Luja 7, шелковисто-матовая, подготовка К3	Tikkurila F497 «Paper»	7,4 м²
О15	плинтус	керамогранит, аналог: плинтус из керамогранита пола, подрезка 80 мм, верхняя кромка с запилом 45°	#B8AFA5 «тон Claystone V486»	2,2 м

Схема развёрток (М 1:50)

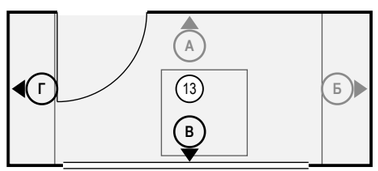

Ведомость изделий и проёмов (на листе)

Стена	Марка	Изделие, проём	На виде Ш×В, мм	Низ, мм
В	М-41	шкаф хозяйственный балконный	385×2000	0
В	М-43	кресло балконное	700×780	0
В	М-42	шкаф хозяйственный балконный	365×2000	0
Г	М-42	шкаф хозяйственный балконный	1220×2000	0

Примечания

1. Размеры — в мм от чистовых поверхностей стен; условные обозначения и общие указания — лист 19.
2. Карнизы (шины) — по ведомости текстиля декоратора: длина L и верх H на развёртке — те же числа, что в ведомости; крепление — до окраски потолка.

	Лист	№ док.	Подпись	Дата
Дизайнер	Кырлан А.С.			14.11.26
Проверил				
Н. контр.				
Утв.				

Проект: Четырёхкомнатная квартира — М 1:20

Развёртки стен В, Г. Балкон 1 (пом. 13)

Стадия	Лист	Листов
П	106	147

выпуск 14.11.2026 № e7147312ff · стр. 106 из 147

Комплект предварительный по пунктам этих таблиц. Пока по пункту нет ответа или решения, показанное на указанном листе — допущение проектировщика, а не утверждённое решение.
Сводка: открытых вопросов — 28 (из них ждут факта объекта — 15: контрольного обмера, обследования или документа); конфликтов между разделами — 1; изменений в реестре — 22, из них без подписи — 1; разделов, не сданных к выпуску, — 1.

Открытые вопросы и принятые допущения

№	Формулировка	Вид	Кто решает	Если решения нет	Лист, где это проявляется
К-1	Окно детской 2 (поз. 9) на наружной стене В: привязки 1580…3080 в источниках нет — в экспликации скана окна этой комнаты не показано. Это допущение проектировщика, центровка, а не замер: окно 1500 мм поставлено примерно по центру наружного участка стены В (по контуру 8030–10610 по оси Х, центр 9320; окно 8540–10040, центр 9290). Размер 1500×1600 и подоконник 800 мм взяты из исходной записи окна, источник размера в данных не указан. Из допущения следует конфликт со стояками Ст К1-2 и Ст В1-2 (9400; 6300) и (9560; 6300): они попадают в проём окна вместе с коробом и люком (конфликт Кф-1, вопрос К-15). Нужен контрольный обмер эркера: положение, размер и подоконник окна, затем осей стояков.	Непонятно Ждёт: обмера	Архитектор-планировщик	Остаётся принятое положение окна как допущение, не замер. Конфликт со стояками Кф-1 не снят: радиатор под окном, шторы и короб со стояками на этом месте не совмещаются.	л. 22 — План планировки от заказчика
К-3	Несущие стены не определены (нет плана БТИ и техзаключения): до их получения демонтаж не планируется. Нужно: запросить проект дома и поэтажный план БТИ, установить серию дома; несущие стены и допустимость вмешательства определяет техническое заключение специализированной организации. Тип дома (монолит) и перекрытие (монолитная плита 220 мм) в данных приняты допущением: источника — проекта дома, плана БТИ, обследования — в материалах объекта нет; материал основания стен и перекрытия определит тот же документ или обследование.	Отсутствует Ждёт: документа, обследования	Архитектор-планировщик	Исходных данных нет: на листе нет решения по этому пункту или оно условное; лист предварительный.	полный альбом
К-4	Гостиная (поз. 11): мебели в модели нет, расстановка ждёт решения заказчика. Отделка, потолок, свет, розетки и декор выполнены; акцентная стена А L481 возвращена (см. К-7); картина ДК20, ваза ДК21 и подсветка картины — предложение конвейера (ИЗ-7). Площадь по модели 14,55 м² (≈17 м² по реконструкции контура — снимет контрольный обмер).	Отсутствует Ждёт: решения	Дизайнер интерьера	Исходных данных нет: на листе нет решения по этому пункту или оно условное; лист предварительный.	л. 32 — План размещения мебели и оборудования
К-5	Гардеробная 1 (поз. 12) в натуре трапеция 2320/2132/1400, в модели прямоугольник той же площади: нужен контрольный обмер углов.	Непонятно Ждёт: обмера	Архитектор-планировщик	Остаётся значение, принятое по исходным данным; оно не подтверждено, лист предварительный.	л. 22 — План планировки от заказчика
К-6	Розетка Р7 (стиральная машина, ванная комната) стоит в 72 мм от угла при норме от 150 мм. Р7 возвращена на прежнее место: стена В, смещение 2543 мм, высота 949 мм — норма ПУЭ 6.6.30 (не выше 1 м) выполнена, флага решения нет; конвейер уходил от угла переносом на 2242 мм и высоту 1250 мм, что нарушало ПУЭ 6.6.30, — этот перенос отменён. Нужно решение автора: сдвинуть машину и розетку от угла или принять 72 мм. Норма для розеток ванной (ПУЭ 7.1.48 против BS 7671) решена: ИЗ-19.	Спорно Ждёт: решения	Инженер-электрик	Р7 остаётся на 2543 мм вдоль стены и 949 мм по высоте, в 72 мм от угла: замечание открыто.	л. 60 — План розеток и электровыводов
К-7	Акцент L481 занимает больше порога 15 % площади поверхностей на акцентной стене А Гостиной — 16 % (проверка по доле акцента, замечание открыто намеренно). Красить плоскость целиком (нужна поддержка в модели), перенести акцент на предметы (в Гостиной они уже есть — ДК20, ДК21, ИЗ-7) или принять 16 %. Для Зала решение принято: 18 % приняты автором (ИЗ-15).	Спорно Ждёт: решения	Колорист-комплектатор	Остаётся акцентная стена L481 в Гостиной, доля 16 % выше порога 15 %; замечание открыто.	л. 30, 31 — Колерная карта
К-8	Графы «Пров.» и «Н. контр.» в штампе пусты: их заполняет человек, подписи проверяющего и нормоконтролёра автор проекта не ставит; для выдачи нужны разные подписанты, отличные от разработчика. Решение автора (ИЗ-18): графы остаются пустыми, комплект предварительный.	Отсутствует Ждёт: решения	Нормоконтролёр	графы остаются пустыми; комплект предварительный, не проверен независимо	л. 19 — Список листов
К-10	Прямые углы помещений с кухней, санузлами, гардеробными и встроенной мебелью по скану не подтверждены (скос стен приведён к ступеням): ванная комната, тёмная комната, детская 1, коридор, кухня, прихожая-коридор, гардеробная 2, детская 2, гардеробная 1, балкон 1. Нужен контрольный обмер: длины сторон, обе диагонали, отклонения углов от 90° у стен под встроенную мебель и плитку; только после него отмечаются углы 90°.	Отсутствует Ждёт: обмера	Архитектор-планировщик	Исходных данных нет: на листе нет решения по этому пункту или оно условное; лист предварительный.	л. 22 — План планировки от заказчика
К-12	Состав подрядчиков и поставщиков (кто покупает и кто монтирует радиаторы, подоконники, двери, розетки) от заказчика не получен. Принята типовая схема частного ремонта (ИЗ-17): материалы и оборудование покупает заказчик по спецификациям проекта, монтаж ведёт подрядная бригада, приёмку скрытых работ ведёт автор. Схема уточняется договором подряда: нужен договор или состав подрядчиков и поставщиков от заказчика.	Отсутствует Ждёт: решения	Прораб-координатор	остаётся типовая схема: покупает заказчик, монтирует подрядная бригада, скрытые работы принимает автор; закрепление за конкретными подрядчиками не подтверждено	л. 19 — Список листов
К-13	Детская 2: рабочий стол М-37 у стены Б получает боковой свет от окна справа от сидящего; для правши лучше свет слева подтвердить, кто сидит за столом (правша или левша), иначе решить зеркальной расстановкой (нужен перенос двери) либо второй лампой слева.	Спорно Ждёт: решения	Дизайнер интерьера	Остаётся вариант, показанный на листе; он не утверждён, лист предварительный.	л. 32 — План размещения мебели и оборудования

	Лист	№ док.	Подпись	Дата	Проект: Четырёхкомнатная квартира			
Дизайнер	Кырлан А.С.			14.11.26	Открытые вопросы, принятые допущения и конфликты. Лист 1 из 6	Стадия	Лист	Листов
Проверил						П	107	147
Н. контр.								
Утв.								

выпуск 14.11.2026 № e7147312ff · стр. 107 из 147

Открытые вопросы и принятые допущения (продолжение)

№	Формулировка	Вид	Кто решает	Если решения нет	Лист, где это проявляется
К-14	Из чего стены под навесными шкафами — Ванная комната (стена Б, М-07), Кухня (стена А, М-23, М-24, М-25), Гардеробная 2 (стена В, М-34)? Проекта дома нет, на скане материал и толщина не читаются. Нужно обследование: материал основания определяет крепёж (анкер по бетону, закладная в ГКЛ). До ответа материал в данных не указан, замечание открыто намеренно.	Отсутствует Ждёт: вскрытия	Мебельщик	Исходных данных нет: на листе нет решения по этому пункту или оно условное; лист предварительный.	л. 24 — Кухня (пом. 6). Монтажная схема л. 25 — Кухня (пом. 6). Монтажная схема л. 26–28 — Шкафы. Монтажная схема
К-15	Стояки Ст К1-2 и Ст В1-2 (в данных (9400; 6300) и (9560; 6300), короб и люк) попадают в проём окна Детской 2 по стене В (8540–10040): совместить с радиатором под окном и шторами нельзя. Привязку осей стояков от двух стен никто не замерял; в Санузле они не стоят, выпуск унитаза С-06 от этого положения — 2,4 м. Нужен контрольный обмер стояков и окна, затем решение: сдвинуть окно, перенести радиатор или обойти короб.	Спорно Ждёт: обмера, затем решения	Инженер ВК (вода, канализация)	Остаются принятые положения окна и стояков без замера; радиатор под окном, шторы и короб со стояками на этом месте не совмещаются.	л. 39 — План выводов сантехники л. 40 — Схема разводки водопровода и канализации л. 22 — План планировки от заказчика
К-17	Ведущий цвет — Paper F497 на стенах и потолке — занимает больше 80 % площади поверхностей в Тёмной комнате (87 %), Гардеробной 2 (89 %), Гардеробной 1 (86 %) и Балконе 1 (85 %): второй цвет почти не читается. Это цвета автора проекта. Принять как есть или задать этим помещениям второй цвет.	Спорно Ждёт: решения	Колорист-комплектатор	Остаются цвета автора: стены и потолок в Paper F497, доля ведущего цвета 85–89 %.	л. 30, 31 — Колерная карта
К-18	Вытяжка М-24 встроена в навесной модуль на отметке 1550 мм: её низ над электрической варочной панелью 610 мм, а фартук 650 мм при практике 450–600 мм. Модель вытяжки не выбрана, паспорта нет, допустимая высота над варочной неизвестна. Поднять модуль М-24 (и соседние М-23, М-25 — на единую отметку), либо выбрать вытяжку, допускающую 610 мм по паспорту.	Спорно Ждёт: данных закупки, затем решения	Мебельщик	Остаётся модуль на отметке 1550 мм; низ вытяжки 610 мм над панелью, меньше 650 мм; допустимость высоты не подтверждена.	л. Д14, Д15 — Д14 Кухня (пом. 6). Развёртка гарнитура
К-19	Привязка угла помещения «Гостиная» (поз. 12 скана; в примечании проекта названо «зал») принята в точке (10670; 3470) мм — это допущение, не замер: по пиксельной привязке скана угол может лежать примерно на 700 мм левее. От этой точки по оси X отсчитываются Гостиная и Гардеробная 1, по ней же проходит стена Детской 2 со стороны Гостиной. Нужен контрольный обмер: расстояние от опорной стены до этого угла.	Непонятно Ждёт: обмера	Архитектор-планировщик	Остаётся угол в точке (10670; 3470) как допущение: размеры правой части на листах — расчётные, возможен сдвиг до ≈700 мм; мебель, свет и розетки там привязаны к принятым координатам.	л. 22 — План планировки от заказчика
К-20	Наружные скошенные стены (в натуре под 45°) заменены на планах ступенями: движок описывает только ортогональную геометрию. Гостиная — три ступени, площадь по модели 14,55 м² против ≈17 м² по реконструкции контура; Гардеробная 1 — прямоугольник 1400×2230 вместо трапеции 2320/2132/1400 той же площади (К-5). Углы и длины скосов на листах не показаны, площади у скошенных стен условные (К-10). Принять ступени как условность до обмера или передать скосы обмером и отдельным чертежом.	Спорно Ждёт: решения	Архитектор-планировщик	Остаются ступени вместо скоса: фактическая форма наружных стен Гостиной и Гардеробной 1 на листах не показана, размеры вдоль скоса брать по обмеру на месте.	л. 22 — План планировки от заказчика л. 32 — План размещения мебели и оборудования
К-21	Все размеры сняты с размерных цепочек растрового скана заказчика, контрольного обмера нет. Площади помещений и «Общая площадь 102,67 м²» в штампе каждого листа — расчётные по модели, не обмерные: итог зависит от ступеней вместо скоса (К-20) и принятого угла Гостиной (К-19). Названия и номера помещений со сканом не сверены (общая комната назначена решением автора, ИЗ-13). Толщины стен приняты допущением: наружные 250 мм, внутренние 120 мм, источника (обмер, проект дома) нет. Всё, что на листах выглядит как замер, снято со скана.	Отсутствует Ждёт: обмера	Архитектор-планировщик	Размеры и площади остаются ориентировочными; штамп печатает «Общая площадь 102,67 м²» как расчётную величину, не подтверждённую обмером; до обмера не заказывать материалы и изделия по размерам листов.	л. 19 — Список листов л. 22 — План планировки от заказчика
К-22	Окно Гостиной (пом. 11) на стене В, часть 2: остекление показано по обмерному скану, размеры 1500×1600 мм и подоконник 900 мм приняты типовыми, не замерены. Нужен контрольный обмер окна: положение, ширина, высота, подоконник.	Непонятно Ждёт: обмера	Архитектор-планировщик	Остаются типовые размеры окна 1500×1600 мм, подоконник 900 мм; на плане они напечатаны как принятые, не замеренные.	л. 22 — План планировки от заказчика
К-23	Две розетки выше 1 м от пола остаются предложением проектировщика, решения автора нет: Р21 (вытяжка М-24, 2200 мм, в модуле за съёмной панелью, Кухня) и Р27 (слаботочный щит ЩС, 1600 мм, Прихожая-коридор). Основание — назначение розетки; автор высоту не подтверждал; основание записано в самой позиции (знак «**» у марки, примечание листа). Норма (ПУЭ, п. 6.6.30) — не выше 1 м. Подтвердить высоты или опустить розетки.	Спорно Ждёт: решения	Инженер-электрик	Высоты остаются как на листе, решение автором не подтверждено.	л. 60 — План розеток и электровыводов полный альбом
К-24	Высота потолка 2700 мм принята: источника (замер, проект дома) в материалах объекта нет. От неё зависят вертикальные размеры альбома: развёртки, шкафы и встроенная мебель, плитка, потолки, объёмы работ. Замерить высоту на объекте в каждом помещении.	Непонятно Ждёт: обмера	Архитектор-планировщик	Высота 2700 мм остаётся принятой, не замеренной: вертикальные размеры листов и объёмы работ ориентировочные; встроенную мебель и плитку по высоте не заказывать до замера.	л. 22 — План планировки от заказчика
К-25	Разрешённая мощность 15 кВт принята, технических условий в материалах объекта нет; расчётная мощность 11,2 кВт. Сверить с техническими условиями.	Непонятно Ждёт: документа	Инженер-электрик	Разрешённая мощность 15 кВт остаётся принятой, не подтверждённой техническими условиями: вводной аппарат и группы щита предварительные.	л. 56, 57 — Однолинейная схема щита

	Лист	№ док.	Подпись	Дата	Проект: Четырёхкомнатная квартира			
Дизайнер	Кырлан А.С.			14.11.26	Открытые вопросы, принятые допущения и конфликты. Лист 2 из 6	Стадия	Лист	Листов
Проверил						П	108	147
Н. контр.								
Утв.								

выпуск 14.11.2026 № e7147312ff · стр. 108 из 147

Открытые вопросы и принятые допущения (продолжение)

№	Формулировка	Вид	Кто решает	Если решения нет	Лист, где это проявляется
К-26	Артикулы изделий отделки не выбраны. Инженерная доска (пом. 1, 3, 4, 6, 8, 9, 11, 12), керамогранит пола (пом. 2, 5, 7, 10, 13), керамогранит стен санузла и ванной (пом. 2, 10) и фартука кухни (пом. 6), плинтус МДФ (пом. 1, 3–9, 11, 12), плинтус из керамогранита (пом. 13) и краска акцентных стен (пом. 1, 11) заданы характеристиками — «аналог по характеристикам», кода изделия производителя нет. Цвет керамогранита назван тоном по колерной карте (J484, F497, V486), но тон — не артикул изделия. Артикул выбирается при закупке: выбрать изделия, вписать артикулы в ведомость отделки и спецификации, цвет и тон принять по образцу из партии. Количество к заказу и упаковки — расчётные, по номинальным размерам, до выбора изделия.	Отсутствует Ждёт: данных закупки, затем решения	Отделочник	материалы остаются описанными характеристиками; заказ по спецификации и подсчёт упаковок — только после выбора изделий	л. 68 — Раскладка плитки. Планы полов л. 69 — Раскладка плитки. Фартук кухни л. 47 — Раскладка плитки. Ванная комната. Развёртки стен л. 48 — Раскладка плитки. Санузел. Развёртки стен л. 67 — План покрытий пола л. С1, С2 — С1–С2 Ведомость отделки помещений л. 30, 31 — Колерная карта л. С3, С4 — С3–С4 Спецификация отделочных материалов полный альбом
К-27	Модели встраиваемой техники кухни не выбраны: холодильник (М-19), духовой шкаф (М-21) и посудомоечная машина (М-26) заданы описанием «аналог по характеристикам» — без производителя, серии и кода. Размеры ниш и вентзазоры взяты по типовой схеме на 600 мм, а не по паспорту модели: у разных изготовителей они расходятся, и модуль, сделанный по типовой нише, может не принять выбранную технику. Вытяжка М-24 — отдельный вопрос К-18. Нужно: выбрать модели, получить монтажные схемы изготовителей и сверить ниши модулей, вентиляцию и подключение до заказа гарнитура.	Отсутствует Ждёт: данных закупки, затем решения	Мебельщик	ниши остаются по типовой схеме на 600 мм, не подтверждённой паспортом модели; модули кухни не заказывать до выбора техники	л. Д14, Д15 — Д14 Кухня (пом. 6). Развёртка гарнитура л. 24 — Кухня (пом. 6). Монтажная схема
К-28	Санузел (пом. 10): унитаз С-06 при положении стояков по данным (К-15) имеет выпуск 3600 мм до стояка К1 и 2357 мм до стояка Ø110 по прямой; вход в санузел — только из Детской 2. Длинный выпуск требует нормативного уклона по всей длине (СП 30.13330) — подъёма пола санузла (подиум) или насосной установки. Решить: принять длинный выпуск с подиумом/насосом, перенести унитаз ближе к стояку или перепланировать санузел — после контрольного обмера стояков (К-15).	Спорно Ждёт: решения	Инженер ВК (вода, канализация)	выпуск С-06 остаётся 3600 мм: раскладка санузла и высота пола не утверждены, разводку канализации не выполнять до решения	л. 39 — План выводов сантехники л. 32 — План размещения мебели и оборудования л. 22 — План планировки от заказчика
К-29	Мойка кухонная С-05 (пом. 6 «Кухня»), выпуск К1-5 Ø50: в полу не помещается: врезка + перепад 202 (10,10 м × 20 мм/м) + Ø50 + слой над трубой 45 = 307 мм при пироге 170 мм. Решить: (а) подиум или подъём пола на 140 мм (ступень на входе — порог); (б) прибор ближе к стояку Ст К1-2; (в) насосная установка (КНС) у прибора — по паспорту, требует согласования. Решение меняет кухню (модули, цоколь, точки ЭОМ) — за автором с заказчиком.	Спорно Ждёт: решения	Инженер ВК (вода, канализация)	выпуск К1-5 и кухню в части мойки не выполнять до решения; остальное — по листам	л. 40 — Схема разводки водопровода и канализации л. 39 — План выводов сантехники
К-30	Посудомоечная машина ОБ-03 (пом. 6 «Кухня»), выпуск К1-6 Ø50: в полу не помещается: врезка + перепад 152 (7,60 м × 20 мм/м) + Ø50 + слой над трубой 45 = 257 мм при пироге 170 мм. Решить: (а) подиум или подъём пола на 90 мм (ступень на входе — порог); (б) прибор ближе к стояку Ст К1-2; (в) насосная установка (КНС) у прибора — по паспорту, требует согласования. Решение меняет кухню (модули, цоколь, точки ЭОМ) — за автором с заказчиком.	Спорно Ждёт: решения	Инженер ВК (вода, канализация)	выпуск К1-6 и кухню в части мойки не выполнять до решения; остальное — по листам	л. 40 — Схема разводки водопровода и канализации л. 39 — План выводов сантехники
К-31	Гостиная (пом. 11, 14,55 м²) в данных без двери и проёма: со всех сторон глухие стены (к детской 1 — стена А, к детской 2 — стена Г, к гардеробной 1 — стена Б), единственная дверь Д-4 ведёт из неё в гардеробную 1, у которой другого выхода нет — два помещения недостижимы из квартиры, при этом в них заведены розетки, свет, LAN и Wi-Fi. По скану внутренней стала стена Б детской 2 на участке 3530…5010 — возможно, там проём; но на этой стене утверждённая расстановка детской 2 (стеллаж М-39, стол М-37, выключатель S18 — ИЗ-1, ИЗ-2). Нужно: выяснить у заказчика вход в гостиную (из детской 2, из детской 1 или новый проём из коридора через перепланировку) и подтвердить обмером; до ответа дверь в данные не вносится.	Отсутствует Ждёт: обследования, затем решения	Архитектор-планировщик	гостиная и гардеробная 1 недостижимы: отделку, потолок, ЭОМ и мебель в них не выполнять; если вход — через детскую 2, расстановку детской 2 (ИЗ-1, ИЗ-2) пересматривать	л. 22 — План планировки от заказчика л. 49 — План размещения дверей л. 32 — План размещения мебели и оборудования
К-32	Помещение «Детская 1»: выключатель основного света L13 не у входа — свет включают только прикроватные выключатели (S3), выключателя у входа нет. Варианты: (а) петли на другую сторону — ручка уходит от угла, выключатель встаёт у ручки; (б) шкаф или тумбу у двери сдвинуть на 300 мм — место освобождается; (в) проходной выключатель у входа в пару к прикроватному — по согласованию с заказчиком; (г) оставить как есть.	Спорно Ждёт: решения	Инженер-электрик	выключатель у входа не закладывать до решения; прикроватные остаются	л. 64 — Управление светильниками

Конфликты между разделами

№	Формулировка	Разделы	Статус	Кто решает	Если решения нет	Лист, где это проявляется
Кф-1	Стояки Ст К1-2, Ст В1-2 с коробом и люком попадают в проём окна Детской 2 (стена В, 8540–10040): положение стояков и окна не замерено; вопрос К-15.	ВК; архитектура (окно Детской 2)	Открыт, круг 1	Инженер ВК (вода, канализация)	Положение окна — допущение, стояков — по скану без привязки; пока их не замерили, окно, радиатор под ним и короб со стояками на листах не согласованы.	л. 39 — План выводов сантехники л. 40 — Схема разводки водопровода и канализации

	Лист	№ док.	Подпись	Дата	Проект: Четырёхкомнатная квартира			
Дизайнер	Кырлан А.С.			14.11.26	Открытые вопросы, принятые допущения и конфликты. Лист 3 из 6	Стадия	Лист	Листов
Проверил						П	109	147
Н. контр.								
Утв.								

выпуск 14.11.2026 № e7147312ff · стр. 109 из 147

Изменения проекта после выпуска листов (реестр изменений)

№	Дата	Лист	Было	Стало	Кто решил, подпись
ИЗ-1	05.10.2026	л. 32 — План размещения мебели и оборудования	Окно Детской 2 на стене Б (смещение 900). Стол М-37 1400×650, стена Б, смещение 1000; кресло М-38 (9300; 4950); стеллаж М-39 1200×2100, стена В, смещение 960.	Окно на наружной стене В (1580…3080; положение — допущение, центровка, не замер). Стол М-37 1400×650 (размер и допуск глубины «Г 600–700» прежние), стена Б, смещение 1500; кресло М-38 (9150; 5450); стеллаж М-39 1200×2100 (размер прежний), стена Б, смещение 120. Основания. Стеллаж: на стене В теперь окно, прежнее место перекрывает проём; на стене Б он стоит в углу А/Б. Стол: перенесён вслед за окном на стену Б без изменения размера; при 650 мм край стола заходит на 20 мм в проекцию проёма окна — это не нарушение, принято автором 05.10.2026 (вопрос К-16 закрыт). Вместе с окном изменились: направление паркета в Детской 2 (по оси X → по оси Y, вдоль света от окна), портьеры и римская штора Т16, Т17 (длина, карниз). Декор: спатифиллум ДК16 перенесён с (9900; 6100) на (10200; 4300), основание в данных не записано. Окно, стол М-37, кресло М-38, стеллаж М-39, портьеры Т16, Т17, декор ДК16 и направление паркета помечены знаком предложения.	Утверждено: Кырлан А.С., автор проекта, 05.10.2026 — утверждены положение и размеры мебели «Детской 2»: стол М-37 1400 × 650 (заход края стола на 20 мм в проекцию проёма окна принят), кресло М-38, стеллаж М-39 1200 × 2100. Не утверждены (допущение или предложение): положение окна, портьеры Т16 и Т17, декор ДК16, направление паркета. Предложил: решение автора проекта, оформлено исполнителем по его поручению (запись внесена конвейером).
ИЗ-2	05.10.2026	л. 60 — План розеток и электровыводов л. 62 — План освещения л. 64 — Управление светильниками л. 63 — Техническое задание на подбор светильников	Детская 2: общий свет L15 (шесть спотов), выключатель S14 (L15 и свет санузла). Бра и отдельных линий у кровати и у стола не было.	Добавлены: бра Св63 у изголовья кровати М-35 (стена А, смещение 510, высота 1400 мм, 6 Вт, 2700 К, линия L21) и выключатель S17 (стена А, смещение 1050, высота 900 мм); бра Св67 над рабочим столом М-37 (стена Б, смещение 2200, высота 1300 мм, 7 Вт, 3000 К, линия L22) и выключатель S18 (стена Б, смещение 1410, высота 900 мм). S18 стоял на смещении 1350 мм и оказывался за стеллажом М-39 1200×2100: стеллаж возвращён к прежнему размеру, выключатель перенесён в просвет между стеллажом и столом. Заказчик бра не заказывал, основание в данных не записано; позиции помечены как предложение проектировщика.	Утверждено: Кырлан А.С., автор проекта, 05.10.2026 — утверждён перенос выключателя S18 в просвет между стеллажом М-39 и столом М-37 (стеллаж прежнего размера 1200 × 2100). Не утверждены (предложение проектировщика): бра Св63 и Св67, выключатели S17 и S18 как позиции, линии L21 и L22. Предложил: решение автора проекта, оформлено исполнителем по его поручению (запись внесена конвейером).
ИЗ-3	05.10.2026	л. 62 — План освещения л. 63 — Техническое задание на подбор светильников	Санузел: общий свет L12 (спот Св51), света у зеркала не было.	Добавлен светильник Св64 над зеркалом ДК17 (стена Б, смещение 600, высота 1950 мм, 8 Вт, 3000 К, IP44, драйвер встроен, линия L12, группа 4). Основание: (свет у зеркала в санузле). Заказчик светильник не заказывал; решение исполнителя, знак «**» у Св64 остаётся.	Утверждено: исполнитель по поручению Кырлана А.С., 05.10.2026. Предложил: исполнитель.
ИЗ-4	05.10.2026	л. 64 — Управление светильниками л. 63 — Техническое задание на подбор светильников	Зал: выключатель S2 (лента в карнизе L3) без светорегулятора, сценариев света нет.	В S2 добавлен светорегулятор (тип ТЕ, под диммируемую ленту); записаны четыре сценария света: «Вечер» (L1 0 %, L2 100 %, L3 50 %), «Гости» (100/100/100 %), «Кино» (0/0/20 %), «Уборка» (100/100/0 %). Основание: (гостиная с тремя и более группами света — сценарий; в Зале L1–L3) и (промежуточный уровень — группе на светорегуляторе). Уровни выбрал исполнитель, заказчик их не задавал; знак «**» у S2 остаётся. Сценарии и диммер записаны для Зала; в Гостиной их нет.	Утверждено: исполнитель по поручению Кырлана А.С., 05.10.2026. Предложил: исполнитель.
ИЗ-5	05.10.2026	л. 56, 57 — Однолинейная схема щита л. 60 — План розеток и электровыводов полный альбом	Розетки Гостиной Р36–Р38 — в группе 9 «розетки фартука кухни». Щит ЩРВ-П-54 на 54 модуля, занято 42.	Новая группа 19 «розетки гостиной»: автомат С16, УЗО 30 мА типа А, кабель ВВГнг(А)-LS 3×2,5, 1,0 кВт, длина линии 30 м (оценка, не замер). Щит ЩРВ-П-72 на 72 модуля, занято 44. Основание щита: при 44 занятых модулях резерв ЩРВ-П-54 составил бы 10 модулей (18,5 %) — меньше 20 %. Основание группы 19: (не больше 12 гнёзд на группу 2,5 мм²; практика): с Р36–Р38 в группе 9 было бы 14 гнёзд, осталось 8. Знак «**» у щита и Р36–Р38 остаётся.	Утверждено: Кырлан А.С., 12.11.2026. Предложил: исполнитель.
ИЗ-6	05.10.2026	л. 49 — План размещения дверей л. 32 — План размещения мебели и оборудования	Гардеробная 1: дверь в Гостиную, проём 1420 мм по скану, полотно распашное 1420 мм.	Полотно раздвижное, две створки по 710 мм по накладной направляющей; проём 1420 мм прежний. Основание: распашное полотно 1420 мм в помещении 1400×2230 задевало стеллаж М-40. Заказчик замену не заказывал; решение исполнителя, знак предложения у двери остаётся.	Утверждено: исполнитель по поручению Кырлана А.С., 05.10.2026. Предложил: исполнитель.
ИЗ-7	05.10.2026	полный альбом л. 30, 31 — Колерная карта л. 62 — План освещения л. 64 — Управление светильниками	Гостиная: акцентная стена А в L481 (finish.accent); предметов декора и подсветки картины не было; выключатель S16 одноклавишный (L19).	Конвейер заменял акцентную стену предметами и ради порога снял её; решением от 05.10.2026 акцентная стена А возвращена (доля 16 % выше порога 15 %, замечание открыто, К-7). Предметы оставлены как предложение: картина ДК20 (стена Г, 800×600), ваза ДК21, подсветка картины Св65, Св66 (линия L20), вторая клавиша S16, подсветка помечена как предложение проектировщика. Нужны ли предметы при акцентной стене — решает автор.	Утверждено: Кырлан А.С., 12.11.2026. Предложил: ИИ-конвейер.
ИЗ-8	05.10.2026	л. 22 — План планировки от заказчика л. 60 — План розеток и электровыводов л. 62 — План освещения	Наружный контур: ступени по осям 14780, 7710, 6540, 7970 мм. Прихожая-коридор: розетка Р27 на стене Г, смещение 1990; ИП5 (5600; 3800). Коридор: ИП3 (8500; 3200), выключатель S4 смещение 870. Детская 1: Св20, Св25 по X 14450. Ванная: Св13 по X 7700, дверь смещение 100. Детская 2: Р33 смещение 3140 мм.	Ступени контура 14840, 7770, 6600, 8030 мм (+60 мм): приведены к крайним граням помещений модели (Детская 1, Санузел); после этого окна Гостиной, Детской 1 и Детской 2 лежат на гранях контура. Р27 на стене А, смещение 1750; ИП5 (5500; 4400), ИП3 (8300; 2850). Св20, Св25 по X 14400 и Св13 по X 7600. Дверь ванной смещение 110. Р33 на смещении 1100 мм: прежнее место попало в проём перенесённого окна (ИЗ-1). S4 смещение 880: вслед за дверью ванной (110 вместо 100), зазор от откоса до выключателя прежний, 70 мм. Сдвиги — решение исполнителя; знак «**» у сдвинутых позиций остаётся.	Утверждено: Кырлан А.С., 12.11.2026. Предложил: исполнитель.

выпуск 14.11.2026 № e7147312ff · стр. 110 из 147

Изменения проекта после выпуска листов (реестр изменений) (продолжение)

№	Дата	Лист	Было	Стало	Кто решил, подпись
ИЗ-9	05.10.2026	л. 60 — План розеток и электровыводов л. 62 — План освещения л. 22 — План планировки от заказчика	Слаботочные точки (5 шт.) без слаботочного щита; точек доступа Wi-Fi не было; параметров щита ЩС в данные проекта не было.	Добавлены: слаботочный щит ЩС (Прихожая-коридор, стена А, смещение 1380, высота 1600 мм), точки доступа AP1 (5500; 5000) и AP2 (13000; 4300), кабель U/UTP кат. 6 у LAN4 и в данные проекта, щит ЩС: глубина 150 мм, пластик, вентилируемый, роутер внутри. Основание: (нет щита) и (ориентир две точки доступа на 102 м²). Заказчик слаботочку в таком составе не заказывал; решение исполнителя, знак «**» у ЩС, AP1, AP2 и LAN4 остаётся. Две точки Wi-Fi и тип щита автор не выбирал.	Утверждено: Кырлан А.С., 12.11.2026. Предложил: исполнитель.
ИЗ-10	05.10.2026	л. 60 — План розеток и электровыводов полный альбом	Кухня: розетка Р21 (вытяжка М-24) на высоте 2200 мм, решение, назначение «вытяжка М-24».	Назначение «вытяжка М-24 (в модуле, съёмная панель)» и признак доступа доступ: да. Высота 2200 мм прежняя, знак предложения прежний, флаг «решение» снят: решающего нет; высота автором не подтверждена, вопрос К-23.	Утверждено: Кырлан А.С., 12.11.2026. Предложил: исполнитель.
ИЗ-11	05.10.2026	л. 32 — План размещения мебели и оборудования л. 30, 31 — Колерная карта	Марки декора Д1…Д19 (совпадали с префиксом дверей Д). Образцов колерной карты 10.	Марки декора ДК1…ДК19, позиции не менялись. Добавлен образец № 11 (J484, Tikkurila): отдельный выкрас плинтуса коридора и прихожей на МДФ.	Утверждено: Кырлан А.С., 12.11.2026. Предложил: исполнитель.
ИЗ-12	24.09.2026	л. 60 — План розеток и электровыводов полный альбом	В ванной комнате и санузле не было вывода к вентилятору вытяжки и коробки уравнивания потенциалов.	Добавлены выводы к вентиляторам: ЭВ2 (ВР1, ванная комната) и ЭВ5 (ВР3, санузел) — группа 4, высота 2550 мм, IP44, включение с основным светом, таймер выбега в вентиляторе; коробки уравнивания потенциалов КУП1 (ванная комната) и КУП2 (санузел) — высота 300 мм, у входа, вне зон 0–2. Основание: правила проверки (питание вентилятора вытяжки мокрого помещения) и (КУП в помещении с ванной или душем). Заказчик эти позиции не заказывал; решение исполнителя, ЭВ2, ЭВ5, КУП1 и КУП2 со знаком «**».	Утверждено: исполнитель по поручению Кырлана А.С., 05.10.2026. Предложил: исполнитель.
ИЗ-13	05.10.2026	л. 32 — План размещения мебели и оборудования л. 22 — План планировки от заказчика	Общая комната квартиры не названа: «Зал» (18,16 м²) или «Гостиная» (14,55 м²); если бы общей считалась «Гостиная», норма 16 м² не выполнялась (вопрос К-9).	Общей комнатой назначен «Зал» (18,16 м²): он больше «Гостиной», проходит норму общей комнаты не менее 16 м² (СП 54.13330.2022, п. 5.11) и по концепции интерьера несёт обеденную группу на шесть персон. «Гостиная» (14,55 м²) остаётся второй жилой комнатой: для неё действует норма спальни 8 м², она выполнена. Названия и номера помещений со сканом по-прежнему не сверены (К-21).	Утверждено: Кырлан А.С., автор проекта, 05.10.2026. Предложил: решение автора проекта, оформлено исполнителем по его поручению.
ИЗ-14	05.10.2026	л. 22 — План планировки от заказчика л. 49 — План размещения дверей	Санузел (поз. 10) в эркере соединён только с «Детской 2»: другого входа нет; вход в помещение с унитазом из жилой комнаты расходится с требованием СП 54 (вопрос К-2).	Сохраняется существующее положение: вход в санузел — из «Детской 2», перепланировка с тамбуром не выполняется. Основание: требование СП 54.13330.2022 (формулировка не сверена с первоисточником) не допускает устраивать вход в помещение с унитазом из жилой комнаты; проект нового входа не устраивает, а оставляет существующий. Тамбур отнял бы площадь «Детской 2», а стены до технического заключения считаются несущими (К-3). Существующий вход взят с обмерного скана заказчика, на объекте не проверен (К-21). Это отступление от требования, рассчитанного на новое строительство, принято как существующее положение; проверка по этому пункту остаётся замечанием.	Утверждено: Кырлан А.С., автор проекта, 05.10.2026. Предложил: решение автора проекта, оформлено исполнителем по его поручению.
ИЗ-15	05.10.2026	л. 30, 31 — Колерная карта л. 32 — План размещения мебели и оборудования	Зал: акцентная стена А (ТВ-стена, L481) занимает 18 % площади поверхностей при пороге акцента 15 % (вопрос К-7).	Доля акцента 18 % принята: ТВ-стена А красится в L481 целиком, это замысел автора, на предметы акцент не переносится. Порог 15 % практики 60/30/10 превышен сознательно. Акцентная стена «Гостиной» (16 %) этим решением не затронута — вопрос К-7.	Утверждено: Кырлан А.С., автор проекта, 05.10.2026. Предложил: решение автора проекта, оформлено исполнителем по его поручению.
ИЗ-16	05.10.2026	л. 19 — Список листов	Состав выдачи не подтверждён: разделы пожарного инженера, акустика, технадзора, слаботочки и допуск ГИПа в сводке ролей числились не сданными (вопрос К-11).	Пожарный инженер, акустик и технадзор в заказ частного ремонта квартиры не входят: роли отмечены в сводке ролей пропущенными, с причиной. Слаботочка входит в состав: выпущен лист «План слаботочных сетей»; отдельная ведомость слаботочки (кабельный журнал, состав слаботочного щита) ролью не сдана и остаётся в таблице несданных разделов. Функции ГИП выполняет автор проекта, графа «ГИП» основной надписи заполнена его фамилией; членство в СРО не проверялось.	Утверждено: Кырлан А.С., автор проекта, 05.10.2026. Предложил: решение автора проекта, оформлено исполнителем по его поручению.
ИЗ-17	05.10.2026	л. 19 — Список листов	Матрицы ответственности (делает / поставляет / принимает / хранит) нет; кто покупает и кто монтирует — не определено (вопрос К-12).	Принята типовая схема частного ремонта: материалы и оборудование покупает заказчик по спецификациям проекта; монтаж ведёт подрядная бригада; приёмку скрытых работ ведёт автор проекта. Распределение закреплено по радиаторам, подоконникам, дверям, розеткам и выключателям, сантехническим приборам, светильникам и отделочным материалам. Схема уточняется договором подряда; состав подрядчиков и поставщиков остаётся вопросом К-12.	Утверждено: Кырлан А.С., автор проекта, 05.10.2026. Предложил: решение автора проекта, оформлено исполнителем по его поручению.

Изменения проекта после выпуска листов (реестр изменений) (продолжение)

№	Дата	Лист	Было	Стало	Кто решил, подпись
ИЗ-18	05.10.2026	л. 19 — Список листов	Графы «Пров.» и «Н. контр.» основной надписи пусты (вопрос К-8); как с ними поступать — не записано.	Графы «Пров.» и «Н. контр.» остаются пустыми: независимой проверки и нормоконтроля проекта не было, автор проекта сам себе их не подписывает. Комплект выпускается предварительным: пока нет подписи проверяющего и нормоконтролёра, отличных от разработчика, он не считается окончательным.	Утверждено: Кырлан А.С., автор проекта, 05.10.2026. Предложил: решение автора проекта, оформлено исполнителем по его поручению.
ИЗ-19	05.10.2026	л. 60 — План розеток и электровыводов полный альбом	Розетки ванной Р7 (стиральная машина) и Р8 (фен): по ПУЭ допустимы в зоне 3 через УЗО 30 мА, по британской норме BS 7671 (п. 701.512.3) — дальше 2,5 м от границы зоны 1; какая норма принята — вопрос К-6.	Принята норма ПУЭ (п. 7.1.48): розетки в зоне 3 помещения с ванной допустимы при защите УЗО 30 мА. Положение розеток не менялось. Основание: розетки вне зон 0–2 (до границы зоны 1: Р7 1630 мм, Р8 — 1441 мм), исполнение IP44, группы 14 и 15 защищены УЗО 30 мА типа А. Это сознательное отступление от зарубежной нормы BS 7671: в России она не действует, по ней в таком месте допустима только бритвенная розетка с разделительным трансформатором. Расстояние Р7 до угла (72 мм при норме от 150 мм) этим решением не затронуто — вопрос К-6.	Утверждено: Кырлан А.С., автор проекта, 05.10.2026. Предложил: решение автора проекта, оформлено исполнителем по его поручению.
ИЗ-20	30.10.2026	л. 49 — План размещения дверей л. 89 — Развёртка стены А. Прихожая-коридор (пом. 7) л. 32 — План размещения мебели и оборудования	Проём коридор → прихожая-коридор (стена В коридора, смещение 500) выходил за общую стену: на развёртке стены А прихожей видны 770 из 900 мм. Шкаф-купе М-30 (1700) заканчивался в 60 мм от проёма двери детской 2.	Проём — смещение 300 (целиком в общей стене, знак «*»: положение со скана, К-21). М-30 1600 мм, зазор до проёма 160 мм под наличник. Вход в гостиную — вопрос К-31 с заданием на обследование.	Утверждено: Кырлан А.С., 12.11.2026. Предложил: исполнитель.
ИЗ-21	10.11.2026	л. 32 — План размещения мебели и оборудования	Стеллаж М-39 («Детская 2») без знака предложения, при этом открыта запись К-31, называющая его: на стене Б возможен проём в гостиную, расстановка детской 2 при этом пересматривается.	Стеллажу М-39 возвращён знак предложения (ссылки ИЗ-1 и К-31); положение (стена Б, смещение 120) и размер 1200 × 2100 не менялись. Запись К-31 не закрывалась: закрывает её автор после обследования входа в гостиную. Подпись автора в ИЗ-1 не тронута.	Утверждено: Кырлан А.С., 12.11.2026. Предложил: исполнитель.
ИЗ-22	12.11.2026	полный альбом л. 32 — План размещения мебели и оборудования	Разбор двух критиков по кадрам: «стерильный шоурум, жизни нет»; кухня остров без единого предмета и без стульев; ванна С-01 в кадре без смесителя. У мебели зала ОБ-01, М-04, М-05 записана латунь, а металл квартиры чёрный. «Шкаф распашной, 3 секции» М-15 (1800) на листе изделия чертится с 4 фасадами, «Шкаф-купе, 3 двери» М-30 (1600) — с 2 дверями: чертёж и кадр расходились. Санузлы без текстиля и предметов, в коридоре голая стена.	Ванна С-01 — «акриловая 1700×750, смеситель настенный термостатический». ОБ-01, М-04, М-05 — металл чёрный. М-15 — «4 створки», М-30 — «2 двери» (как на листах изделий; «Комод, 4 ящика» М-16, «Консоль, 3 ящика» М-32, «4 секции» М-36 с данными и листами сходятся). Ванная: банные и ручные полотенца на полотенцесушителе С-04 (Т24, Т25), коврик 800×450 у бортика ванны (Т26; вне полотна двери), ваза и свеча с диффузором на полке короба инсталляции (ДК22, ДК23). Санузел: ваза с сухоцветом на полке короба (ДК24). Прихожая-коридор: керамика на консоли М-32 под зеркалом (ДК25), линогравюра 400×560 на стене В справа от банкетки М-31 (ДК26). Коридор: диптих 2 × 500×700 на стене В напротив шкафа М-18 (ДК27, ДК28; проход 980 мм только настенный декор). Зал: книги и свеча на журнальном столе (ДК29), керамика на буфете (ДК30), ваза на обеденном столе (ДК31); подушек на диване 4 (Т4: 3 → 2). Детская 1: рабочая лампа на столе М-13 (ДК32), книги на тумбе М-11 (ДК33), керамика на комоде М-16 (ДК34). Детская 2: рабочая лампа на столе М-37 (ДК35). Кухня: два полубарных стула у тыльной стороны острова М-26 (М-28, М-29; за стульями до стены 865 мм, дверь на балкон и пенал М-27 свободны), керамика на острове и на столешнице (ДК36, ДК37). Гостиная (поз. 12) не дополнялась: мебели в модели нет, расстановка ждёт решения заказчика. Цвета — из палитры проекта: Silhouette L481, Claystone V486, Paper F497, серо-петроль S 5010-B10G, Green Smoke. Знак «**» у позиций до подписи автора.	Не утверждено: подписи нет. решение исполнителя; предложение проектировщика, на утверждение А. С. Кырлана

Разделы, не сданные к выпуску (сводка ролей)


№	Раздел	Состояние	Причина
1	Инженер слаботочки и умного дома	Не сдан	слаботочка входит в состав заказа (ИЗ-16); выпущен лист «План слаботочных сетей» (раздел электрика); отдельная ведомость слаботочки — кабельный журнал, состав слаботочного щита — не выпущена

Примечания


1. Номера листов — по ведомости рабочих чертежей комплекта (лист «Общие данные»).
2. Графа «Если решения нет» показывает состояние решения на листах; влияние на сроки и стоимость по пунктам не оценивалось.
3. Пункт, по которому принято решение, при следующем выпуске комплекта из таблиц исключается.

	Лист	№ док.	Подпись	Дата	Проект: Четырёхкомнатная квартира			
Дизайнер	Кырлан А.С.			14.11.26	Открытые вопросы, принятые допущения и конфликты. Лист 6 из 6	Стадия	Лист	Листов
Проверил						П	112	147
Н. контр.								
Утв.								


Общий вид (М 1:20)

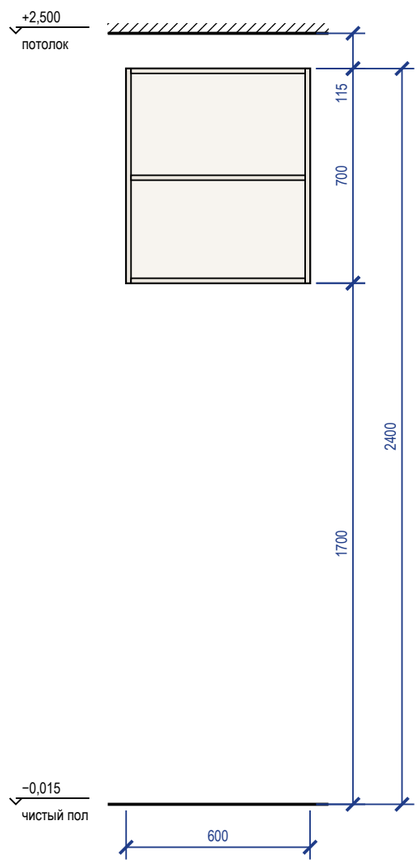

Наполнение, размеры в свету (М 1:20)

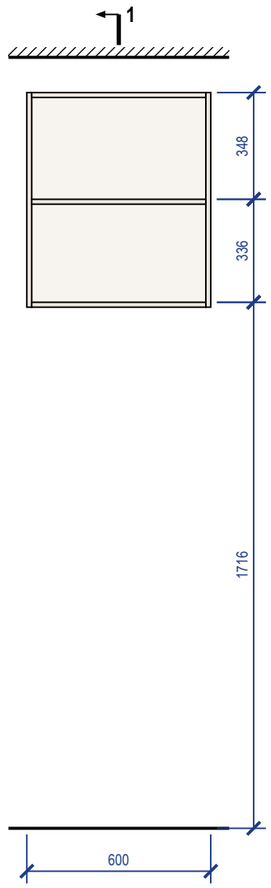


Разрез 1-1 (М 1:20)

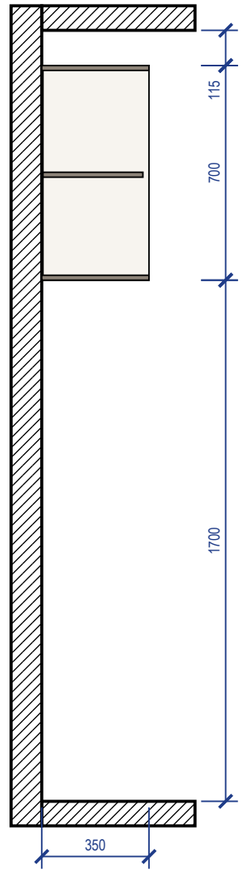

Примечания

1. Размеры — в мм по чистовой отделке; изделие 600×350×700 (Ш×Г×В). Перед раскроем — контрольный замер цеха после чистовой отделки стен, пола и потолка.
2. Корпус — ЛДСП 16 мм, задняя стенка ХДФ 4 мм в паз, навесной корпус без цоколя, низ на 1700 мм от чистого пола; открытая система: без фасадов.
3. Кромка: скрытые торцы 0,4 мм, видимые 2 мм (ПВХ/АБС).
4. Присадка по 32-й системе — выполняет цех.
5. Зазор до потолка 115 мм — закрыть планкой в цвет корпуса при монтаже.
6. Навесной корпус — на стене: крепление к стене, 2 точки; основание стены и шаг анкеров — монтажная схема шкафов.


3D орто

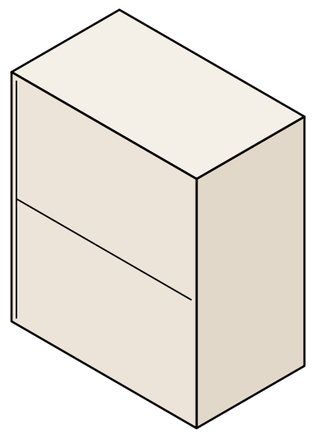


	Лист	№ док.	Подпись	Дата	Проект: Четырёхкомнатная квартира		М 1:20	
Дизайнер	Кырлан А.С.			14.11.26	Система хранения М-07	Стадия	Лист	Листов
Проверил						П	Д1	147
Н. контр.								
Утв.								

выпуск 14.11.2026 № e7147312ff · стр. 113 из 147


Общий вид (М 1:25)

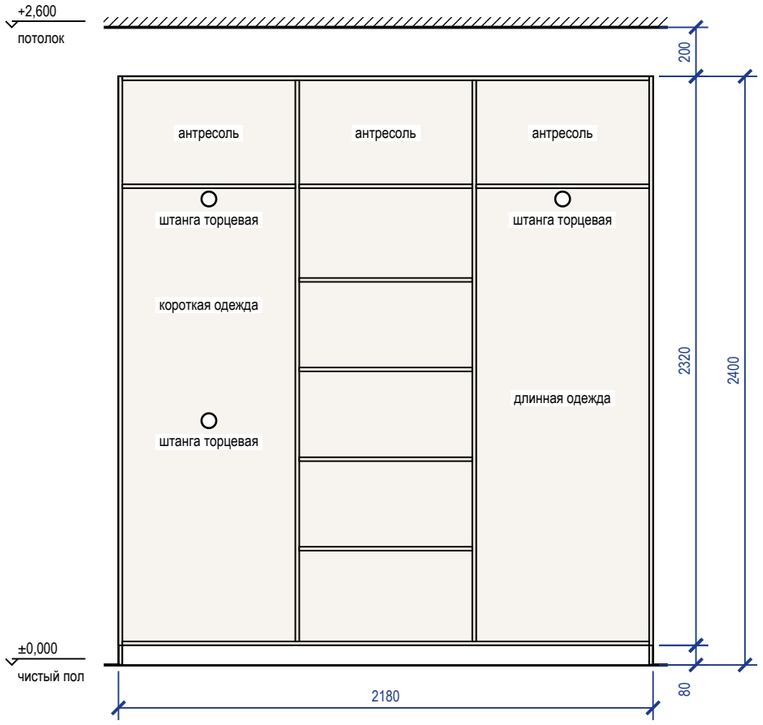


Наполнение, размеры в свету (М 1:25)

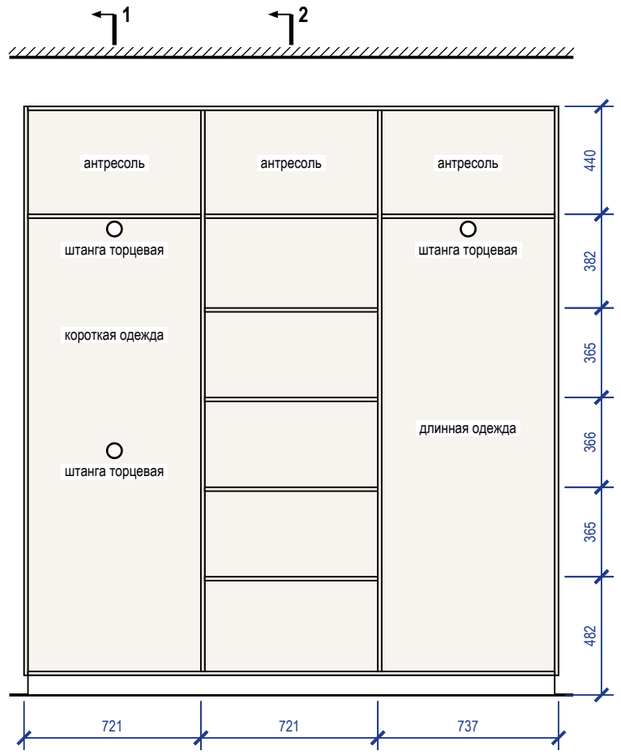

Разрез 1-1 (М 1:25)

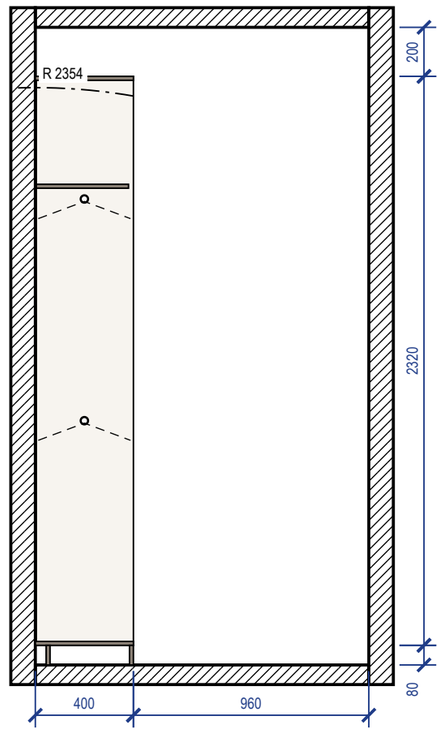


Разрез 2-2 (М 1:25)

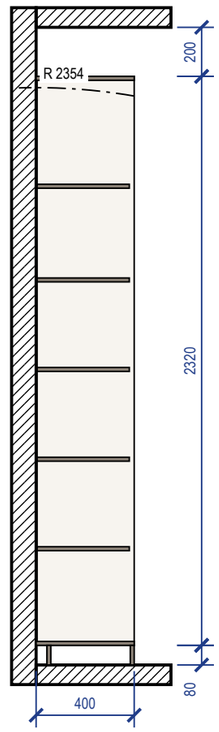

Примечания

1. Размеры — в мм по чистовой отделке; изделие 2180×400×2400 (Ш×Г×В). Перед раскроем — контрольный замер цеха после чистовой отделки стен, пола и потолка.
2. Корпус — ЛДСП 16 мм, задняя стенка ХДФ 4 мм в паз, цоколь 80 мм на регулируемых опорах; открытая система: без фасадов.
3. Кромка: скрытые торцы 0,4 мм, видимые 2 мм (ПВХ/АБС).
4. Присадка по 32-й системе — выполняет цех.
5. Зазор до потолка 200 мм.
6. Подъём корпуса: диагональ боковины без цоколя √(2320² + 400²) = 2354 мм < 2600 мм до потолка — корпус собирается лёжа, поднимается поворотом и ставится на цоколь.
7. Крепление к стене от опрокидывания: крепление к стене, 4 точки; основание стены и шаг анкеров — монтажная схема шкафов.
8. Проход перед изделием 960 мм показан на разрезе 1-1.


3D орто

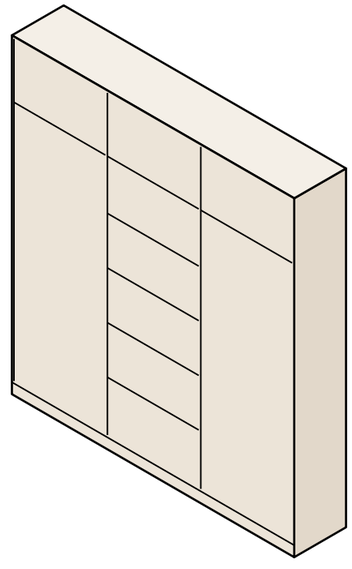

	Лист	№ док.	Подпись	Дата	Проект: Четырёхкомнатная квартира			М 1:25
Дизайнер	Кырлан А.С.			14.11.26	Система хранения М-08	Стадия	Лист	Листов
Проверил						П	Д2	147
Н. контр.								
Утв.								

выпуск 14.11.2026 № e7147312ff · стр. 114 из 147


Общий вид (М 1:20)

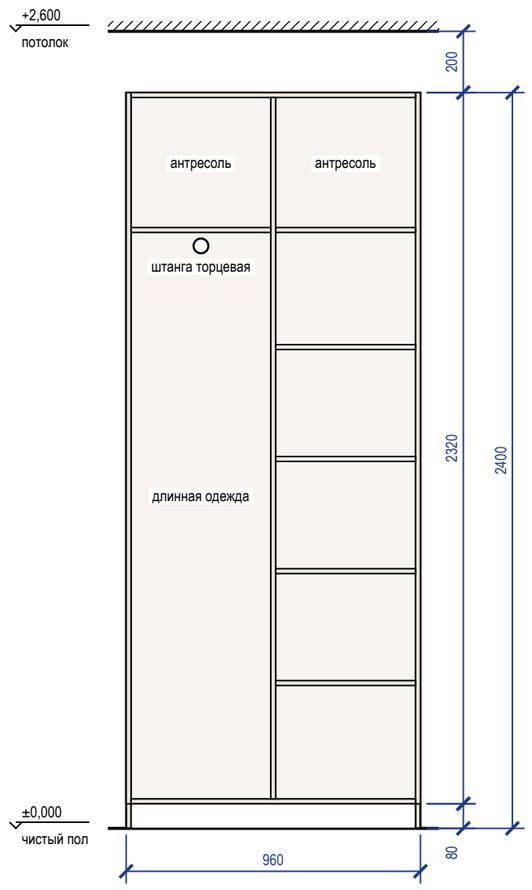


Наполнение, размеры в свету (М 1:20)



Разрез 1-1 (М 1:20)

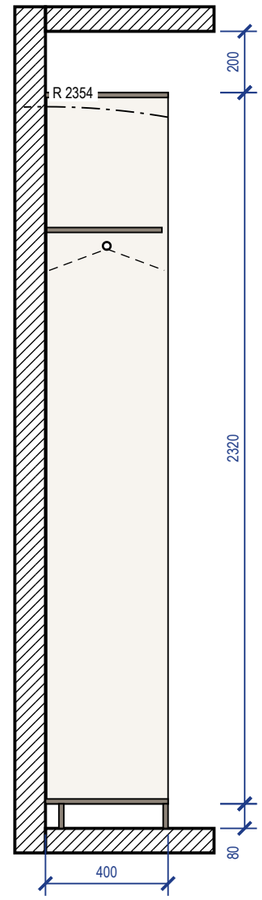


Разрез 2-2 (М 1:20)

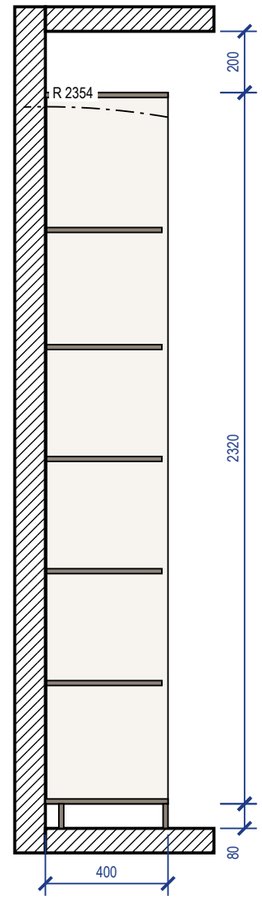

Примечания

1. Размеры — в мм по чистовой отделке; изделие 960×400×2400 (Ш×Г×В). Перед раскроем — контрольный замер цеха после чистовой отделки стен, пола и потолка.
2. Корпус — ЛДСП 16 мм, задняя стенка ХДФ 4 мм в паз, цоколь 80 мм на регулируемых опорах; открытая система: без фасадов.
3. Кромка: скрытые торцы 0,4 мм, видимые 2 мм (ПВХ/АБС).
4. Присадка по 32-й системе — выполняет цех.
5. Зазор до потолка 200 мм.
6. Подъём корпуса: диагональ боковины без цоколя $\sqrt{(2320^2 + 400^2)} = 2354$ мм < 2600 мм до потолка — корпус собирается лёжа, поднимается поворотом и ставится на цоколь.
7. Крепление к стене от опрокидывания: крепление к стене, 3 точки; основание стены и шаг анкеров — монтажная схема шкафов.


3D орто

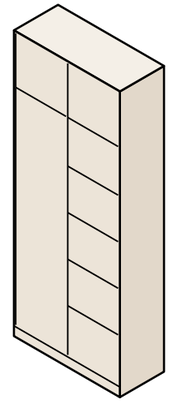


	Лист	№ док.	Подпись	Дата	Проект: Четырёхкомнатная квартира	М 1:20		
Дизайнер	Кырлан А.С.			14.11.26				
Проверил					Система хранения М-09	Стадия	Лист	Листов
Н. контр.						П	Д3	147
Утв.								

выпуск 14.11.2026 № e7147312ff · стр. 115 из 147


Вид с фасадами (М 1:20)

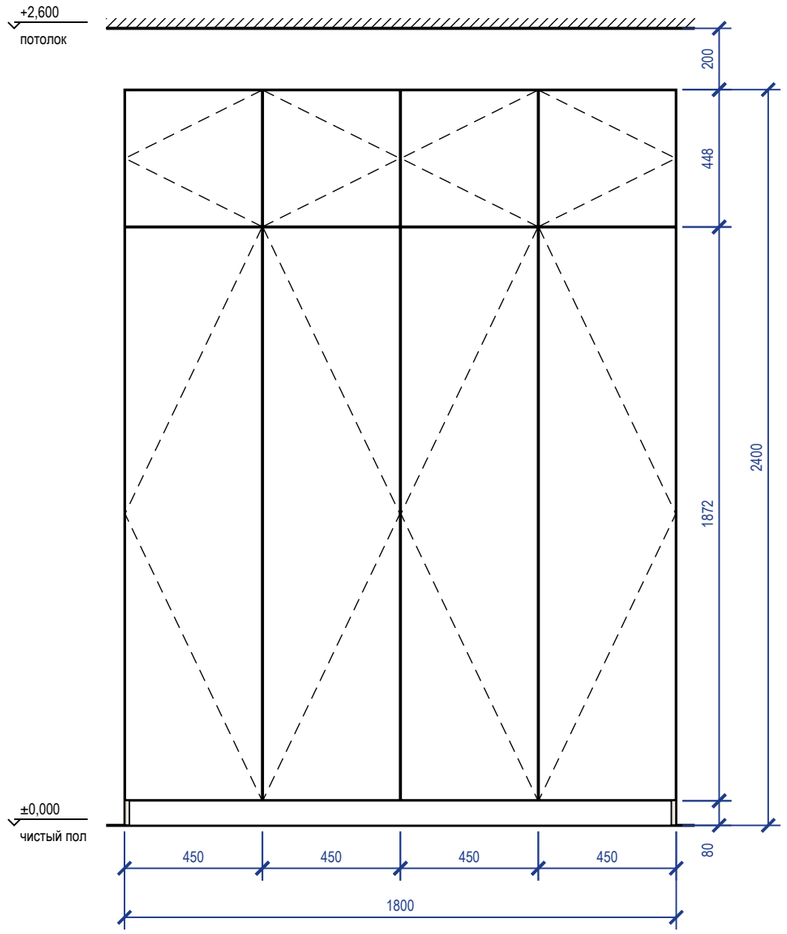


Вид без фасадов (М 1:20)

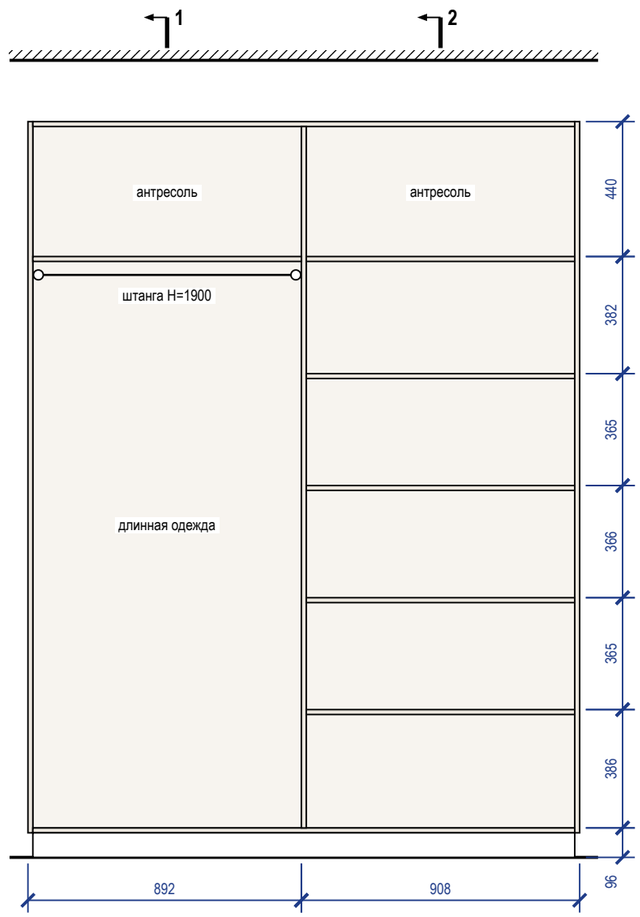

Разрез 1-1 (М 1:20)

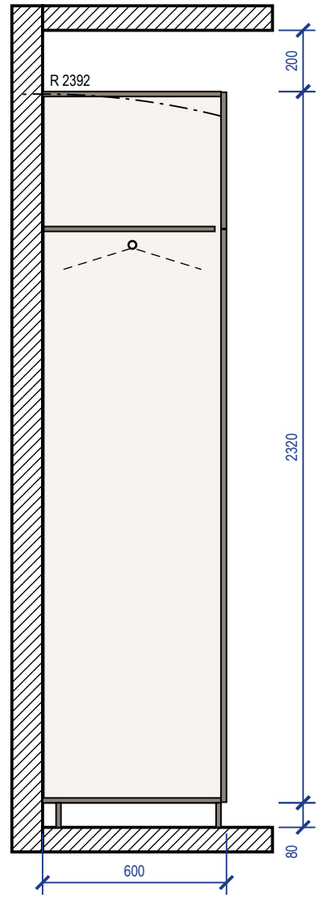


Разрез 2-2 (М 1:20)

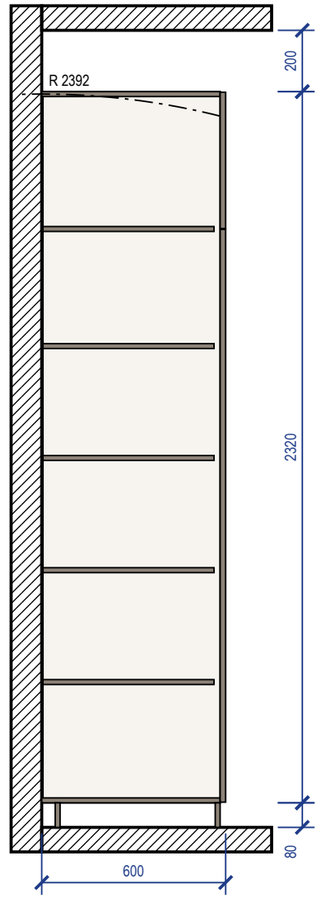

Примечания

1. Размеры — в мм по чистовой отделке; изделие 1800×600×2400 (Ш×Г×В). Перед раскроем — контрольный замер цеха после чистовой отделки стен, пола и потолка.
2. Корпус — ЛДСП 16 мм, задняя стенка ХДФ 4 мм в паз, цоколь 80 мм на регулируемых опорах; фасады накладные — МДФ 18 мм, эмаль матовая, 18 мм; цвет — по колерной карте; петли с доводчиком: фасад 1869 мм — 4 петли, фасад 445 мм — 2 петли.
3. Кромка: скрытые торцы 0,4 мм, видимые 2 мм (ПВХ/АБС).
4. Номинальные зазоры: между фасадами 3 мм, фасад — стена и фасад — потолок не менее 3 мм, фасад ящика — стойка 2 мм.
5. Присадка по 32-й системе — выполняет цех.
6. Зазор до потолка 200 мм.
7. Подъём корпуса: диагональ боковины без цоколя √(2320² + 582²) = 2392 мм < 2600 мм до потолка — корпус собирается лёжа, поднимается поворотом и ставится на цоколь.
8. Крепление к стене от опрокидывания: уголок к стене, 3 шт.; основание стены и шаг анкеров — монтажная схема шкафов.


3D орто

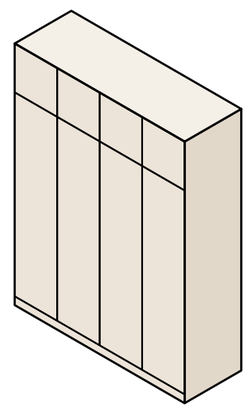


	Лист	№ док.	Подпись	Дата	Проект: Четырёхкомнатная квартира		М 1:20	
Дизайнер	Кырлан А.С.			14.11.26	Шкаф распашной М-15	Стадия	Лист	Листов
Проверил						П	Д4	147
Н. контр.								
Утв.								

выпуск 14.11.2026 № e7147312ff · стр. 116 из 147


Общий вид (М 1:20)

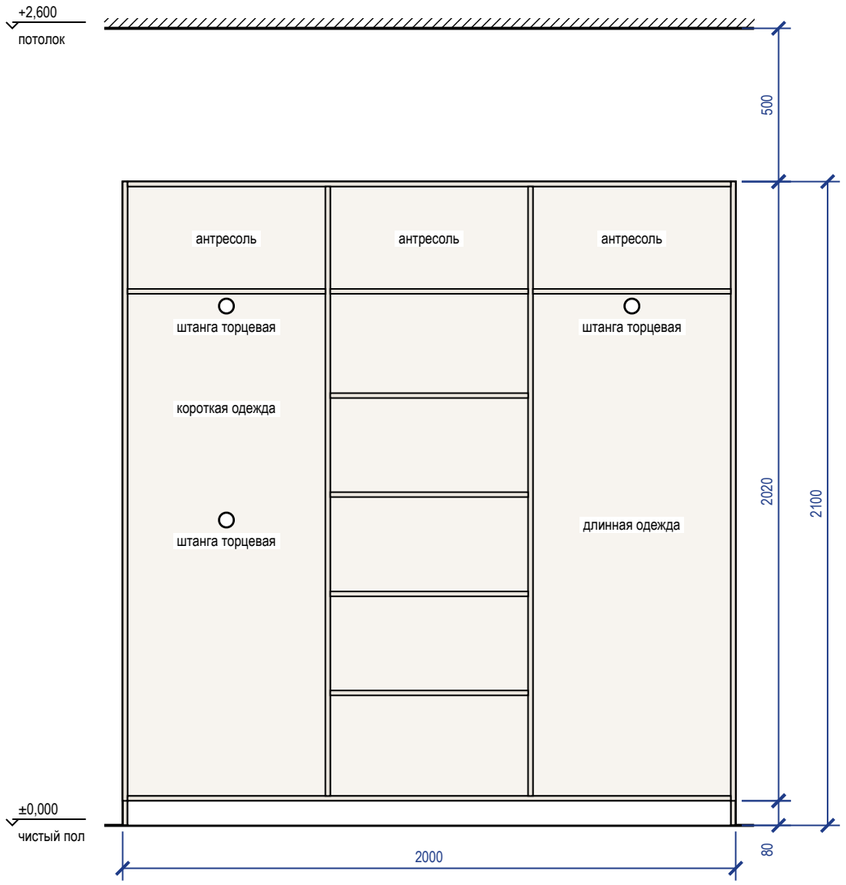


Наполнение, размеры в свету (М 1:20)

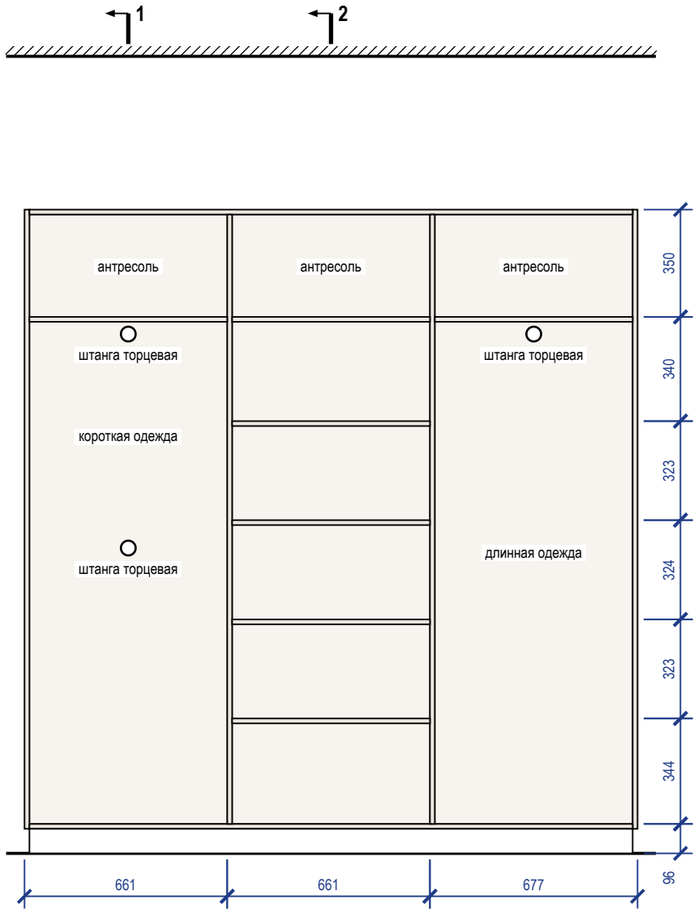

Разрез 1-1 (М 1:20)

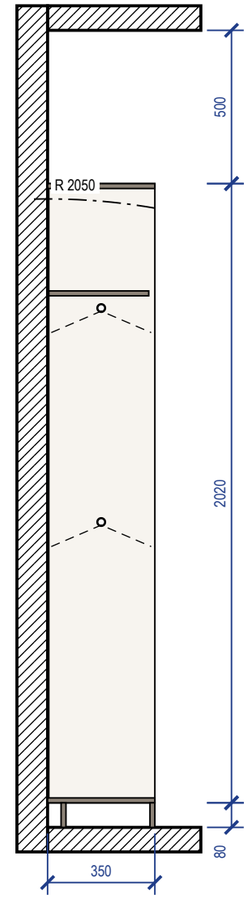


Разрез 2-2 (М 1:20)

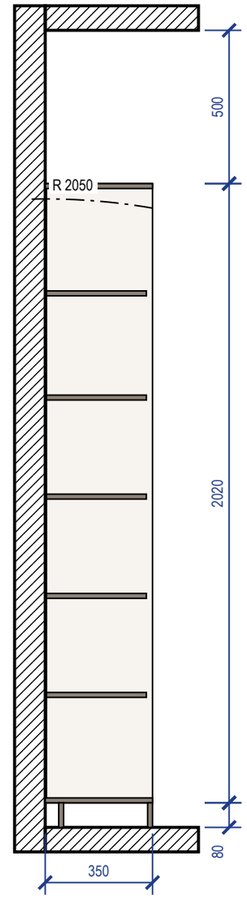

Примечания

1. Размеры — в мм по чистовой отделке; изделие 2000×350×2100 (Ш×Г×В). Перед раскроем — контрольный замер цеха после чистовой отделки стен, пола и потолка.
2. Корпус — ЛДСП 16 мм, задняя стенка ХДФ 4 мм в паз, цоколь 80 мм на регулируемых опорах; открытая система: без фасадов.
3. Кромка: скрытые торцы 0,4 мм, видимые 2 мм (ПВХ/АБС).
4. Присадка по 32-й системе — выполняет цех.
5. Зазор до потолка 500 мм.
6. Подъём корпуса: диагональ боковины без цоколя $\sqrt{(2020^2 + 350^2)} = 2050$ мм < 2600 мм до потолка — корпус собирается лёжа, поднимается поворотом и ставится на цоколь.
7. Крепление к стене от опрокидывания: крепление к стене, 3 точки; основание стены и шаг анкеров — монтажная схема шкафов.


3D орто

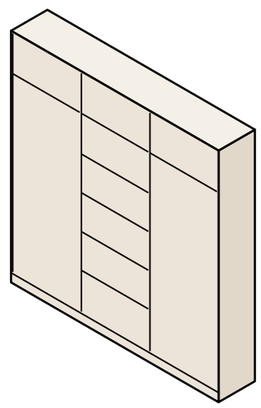


	Лист	№ док.	Подпись	Дата	Проект: Четырёхкомнатная квартира			М 1:20
Дизайнер	Кырлан А.С.			14.11.26	Система хранения М-17	Стадия	Лист	Листов
Проверил						П	Д5	147
Н. контр.								
Утв.								

выпуск 14.11.2026 № e7147312ff · стр. 117 из 147


Вид с фасадами (М 1:20)

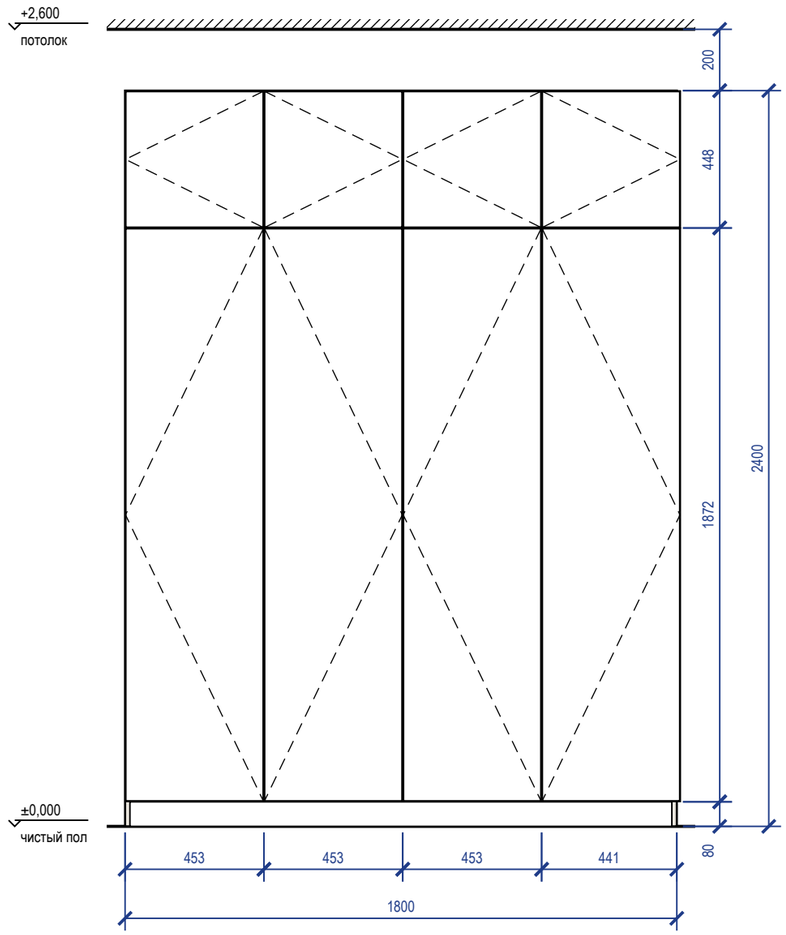

Вид без фасадов (М 1:20)

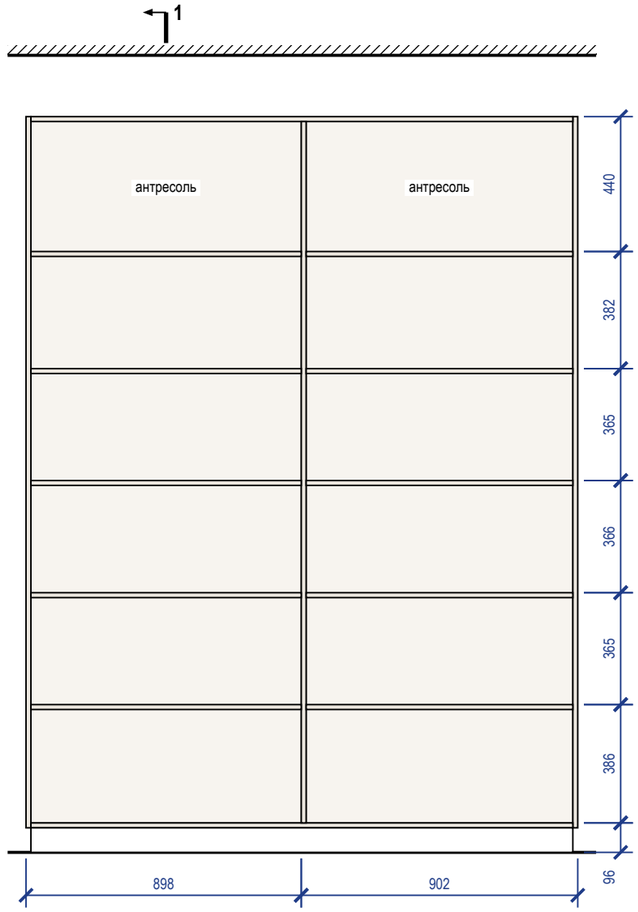


Разрез 1-1 (М 1:20)

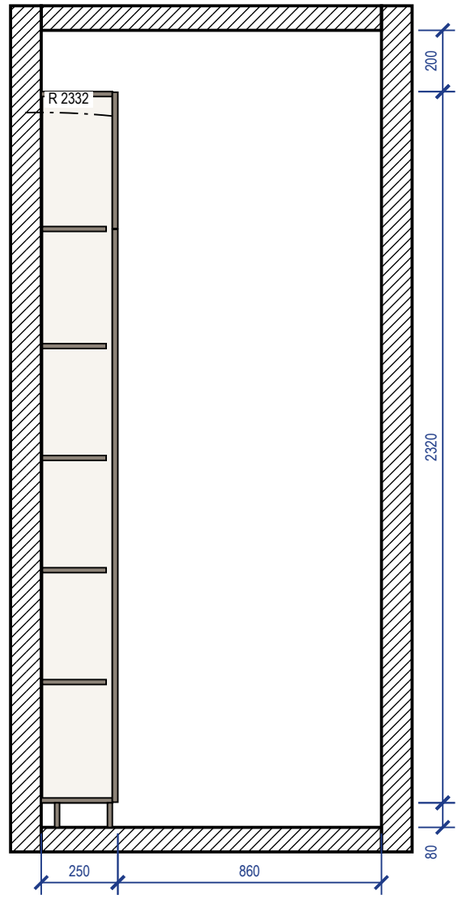

Примечания

1. Размеры — в мм по чистовой отделке; изделие 1800×250×2400 (Ш×Г×В). Перед раскроем — контрольный замер цеха после чистовой отделки стен, пола и потолка.
2. Корпус — ЛДСП 16 мм, задняя стенка ХДФ 4 мм в паз, цоколь 80 мм на регулируемых опорах; фасады накладные — МДФ 18 мм, эмаль матовая, 18 мм; цвет — по колерной карте; петли с доводчиком: фасад 1869 мм — 4 петли, фасад 445 мм — 2 петли.
3. Кромка: скрытые торцы 0,4 мм, видимые 2 мм (ПВХ/АБС).
4. Номинальные зазоры: между фасадами 3 мм, фасад — стена и фасад — потолок не менее 3 мм, фасад ящика — стойка 2 мм.
5. Присадка по 32-й системе — выполняет цех.
6. Зазор до потолка 200 мм.
7. Подъём корпуса: диагональ боковины без цоколя $\sqrt{(2320^2 + 232^2)} = 2332$ мм < 2600 мм до потолка — корпус собирается лёжа, поднимается поворотом и ставится на цоколь.
8. Крепление к стене от опрокидывания: крепление к стене, 4 точки; основание стены и шаг анкеров — монтажная схема шкафов.
9. Проход перед изделием 860 мм показан на разрезе 1-1.


3D орто

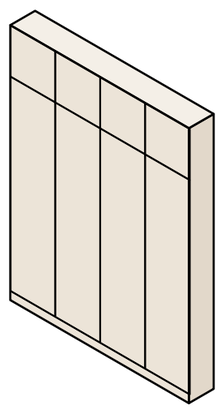


	Лист	№ док.	Подпись	Дата	Проект: Четырёхкомнатная квартира			М 1:20
Дизайнер	Кырлан А.С.			14.11.26	Система хранения М-18	Стадия	Лист	Листов
Проверил						П	Д6	147
Н. контр.								
Утв.								

выпуск 14.11.2026 № e7147312ff · стр. 118 из 147


Вид с фасадами (М 1:20)

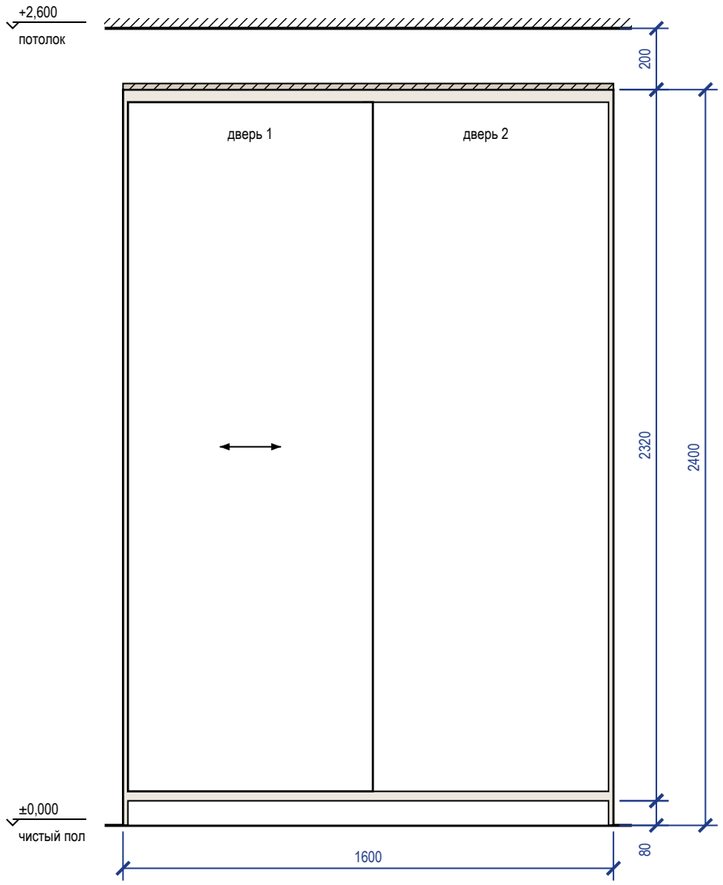


Вид без фасадов (М 1:20)

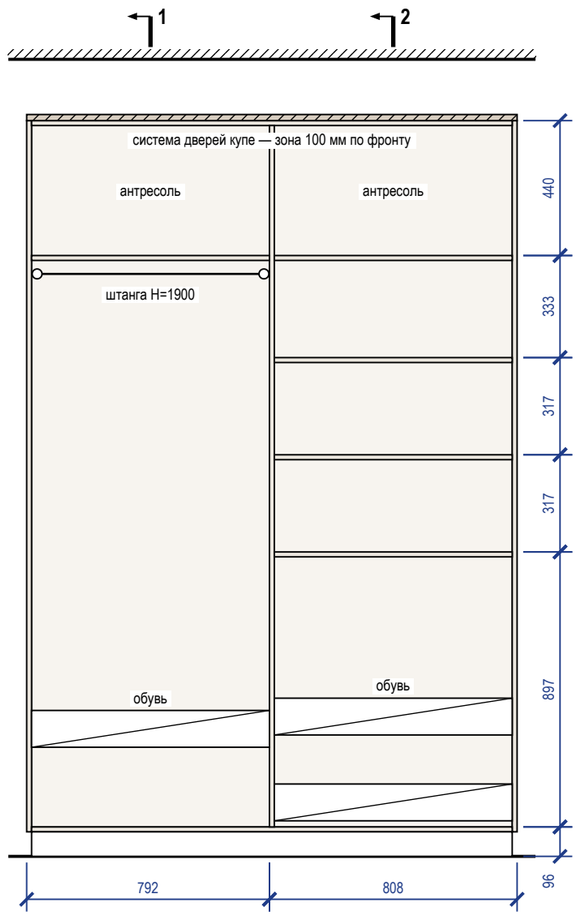

Разрез 1-1 (М 1:20)

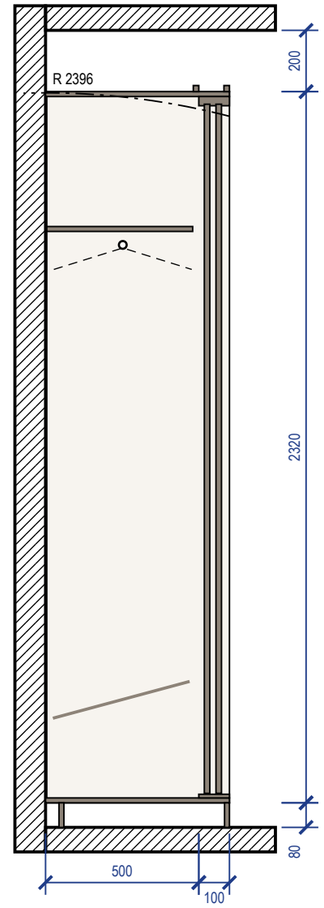


Разрез 2-2 (М 1:20)

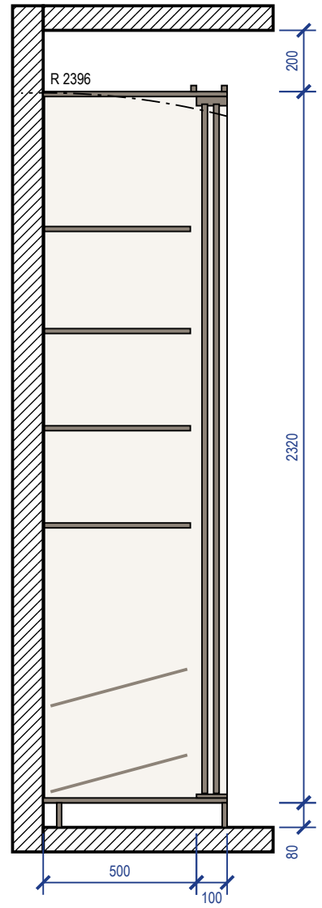

Примечания

1. Размеры — в мм по чистовой отделке; изделие 1600×600×2400 (Ш×Г×В). Перед раскроем — контрольный замер цеха после чистовой отделки стен, пола и потолка.
2. Корпус — ЛДСП 16 мм, задняя стенка ХДФ 4 мм в паз, цоколь 80 мм на регулируемых опорах; двери купе — ЛДСП 10 мм в алюминиевом профиле; нахлёст 30 мм, ширина двери 799 мм, высота — проём минус 40 мм; цвет — по колерной карте.
3. Кромка: скрытые торцы 0,4 мм, видимые 2 мм (ПВХ/АБС).
4. Номинальные зазоры: дверь купе — боковина 3 мм, фасад ящика — стойка 2 мм; ящики внутри купе — с накладкой 30 мм на стойке со стороны нахлёста дверей.
5. Присадка по 32-й системе — выполняет цех.
6. Компенсатор 20 мм — короб из ЛДСП по фронту и торцам, подгоняется к потолку при монтаже (припуск 20 мм), крепится к корпусу и к потолку.
7. Подъём корпуса: диагональ боковины без цоколя $\sqrt{(2320^2 + 600^2)} = 2396$ мм < 2600 мм до потолка — корпус собирается лёжа, поднимается поворотом и ставится на цоколь.
8. Крепление к стене от опрокидывания: крепление к стене, 3 точки; основание стены и шаг анкеров — монтажная схема шкафов.

3D орто

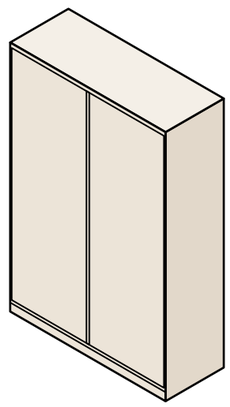

	Лист	№ док.	Подпись	Дата
Дизайнер	Кырлан А.С.			14.11.26
Проверил				
Н. контр.				
Утв.				


Проект: Четырёхкомнатная квартира — **М 1:20**

Шкаф-купе М-30


Стадия	Лист	Листов
П	Д7	147

выпуск 14.11.2026 № e7147312ff · стр. 119 из 147


Общий вид (М 1:20)

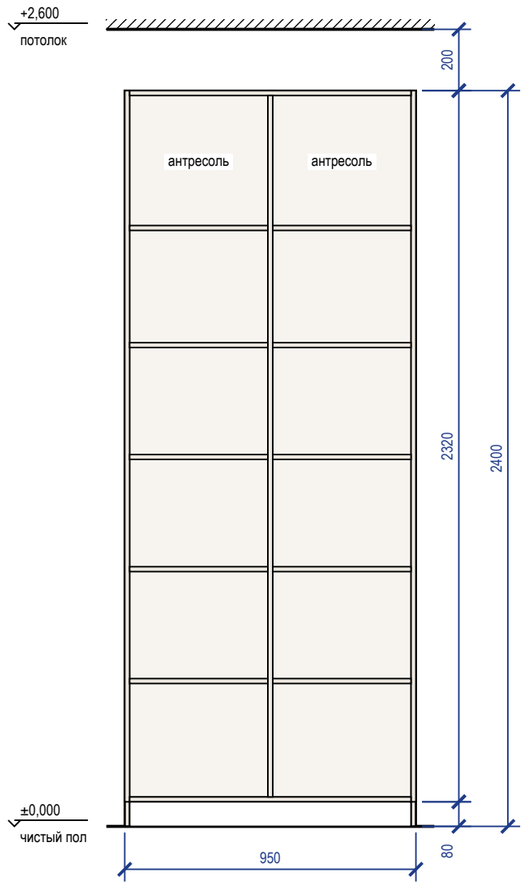

Наполнение, размеры в свету (М 1:20)

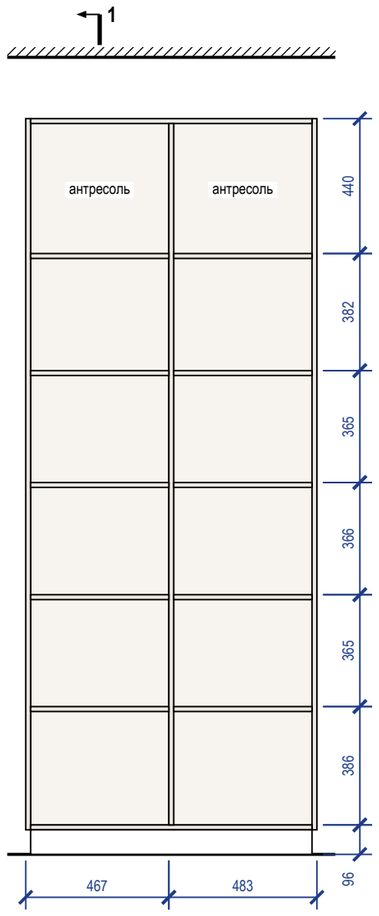


Разрез 1-1 (М 1:20)

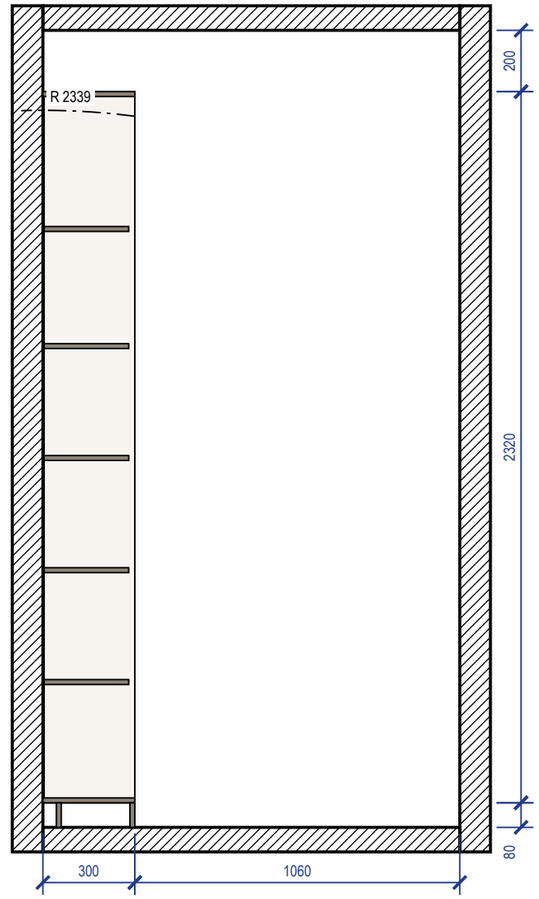

Примечания

1. Размеры — в мм по чистовой отделке; изделие 950×300×2400 (Ш×Г×В). Перед раскроем — контрольный замер цеха после чистовой отделки стен, пола и потолка.
2. Корпус — ЛДСП 16 мм, задняя стенка ХДФ 4 мм в паз, цоколь 80 мм на регулируемых опорах; открытая система: без фасадов.
3. Кромка: скрытые торцы 0,4 мм, видимые 2 мм (ПВХ/АБС).
4. Присадка по 32-й системе — выполняет цех.
5. Зазор до потолка 200 мм.
6. Подъём корпуса: диагональ боковины без цоколя $\sqrt{(2320^2 + 300^2)} = 2339$ мм < 2600 мм до потолка — корпус собирается лёжа, поднимается поворотом и ставится на цоколь.
7. Крепление к стене от опрокидывания: крепление к стене, 3 точки; основание стены и шаг анкеров — монтажная схема шкафов.
8. Проход перед изделием 1060 мм показан на разрезе 1-1.


3D орто

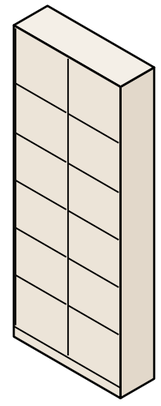


	Лист	№ док.	Подпись	Дата	Проект: Четырёхкомнатная квартира		М 1:20
Дизайнер	Кырлан А.С.			14.11.26			
Проверил					Система хранения М-33	Стадия / Лист / Листов	
Н. контр.						П / Д8 / 147	
Утв.							

выпуск 14.11.2026 № e7147312ff · стр. 120 из 147


Общий вид (М 1:20)

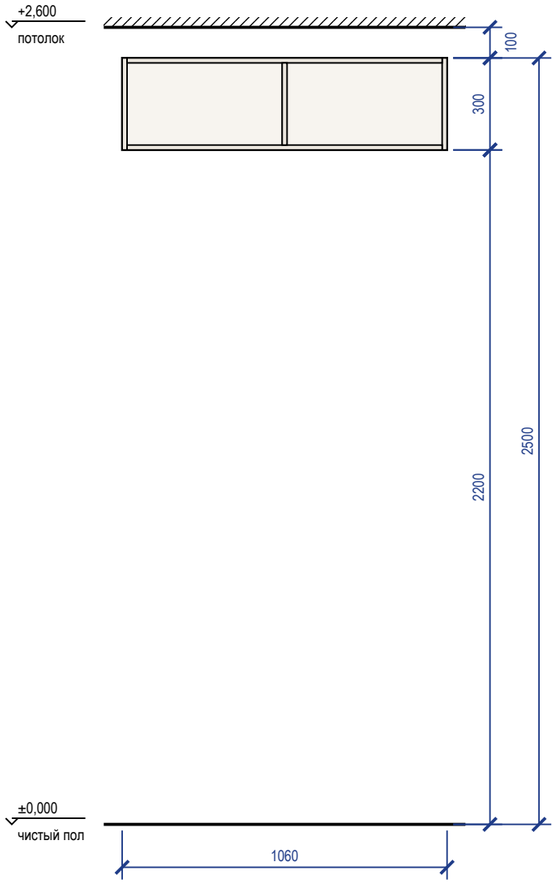

Наполнение, размеры в свету (М 1:20)

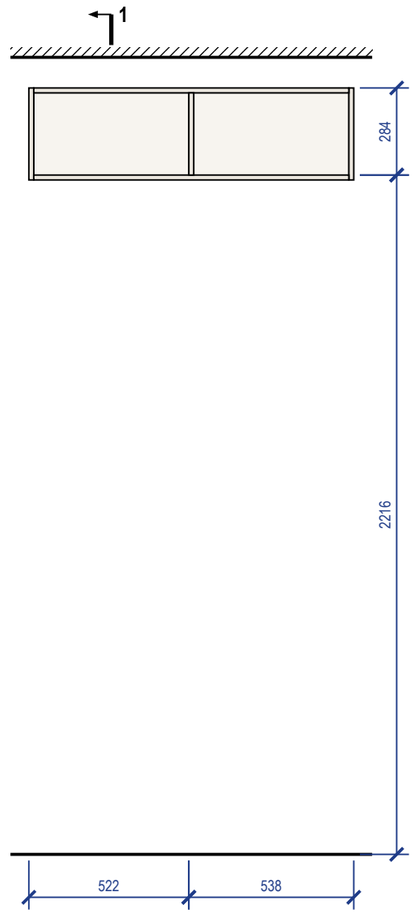


Разрез 1-1 (М 1:20)

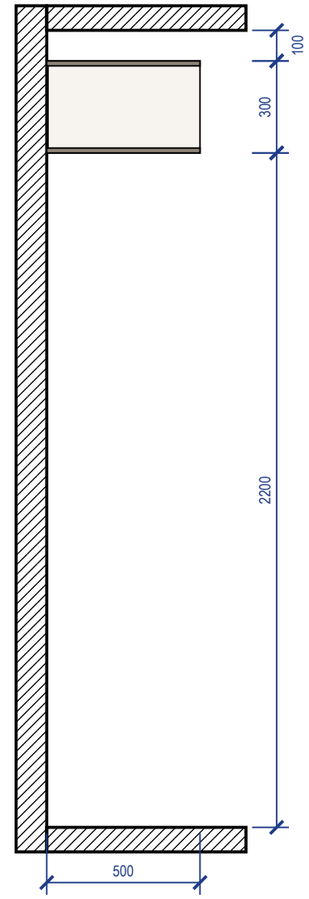

Примечания

1. Размеры — в мм по чистовой отделке; изделие 1060×500×300 (Ш×Г×В). Перед раскроем — контрольный замер цеха после чистовой отделки стен, пола и потолка.
2. Корпус — ЛДСП 16 мм, задняя стенка ХДФ 4 мм в паз, навесной корпус без цоколя, низ на 2200 мм от чистого пола; открытая система: без фасадов.
3. Кромка: скрытые торцы 0,4 мм, видимые 2 мм (ПВХ/АБС).
4. Присадка по 32-й системе — выполняет цех.
5. Зазор до потолка 100 мм — закрыть планкой в цвет корпуса при монтаже.
6. Навесной корпус — на стене: крепление к стене, 4 точки; основание стены и шаг анкеров — монтажная схема шкафов.


3D орто

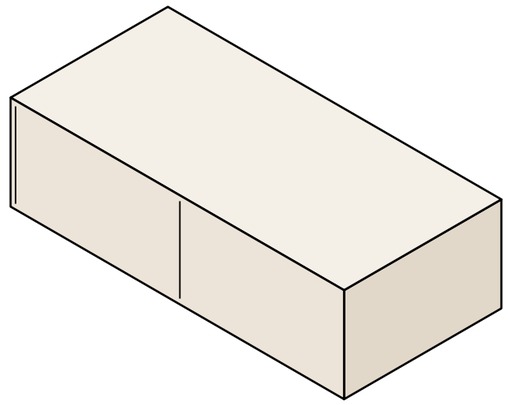


	Лист	№ док.	Подпись	Дата	Проект: Четырёхкомнатная квартира			М 1:20
Дизайнер	Кырлан А.С.			14.11.26	Система хранения М-34	Стадия	Лист	Листов
Проверил						П	Д9	147
Н. контр.								
Утв.								

выпуск 14.11.2026 № e7147312ff · стр. 121 из 147


Вид с фасадами (М 1:20)

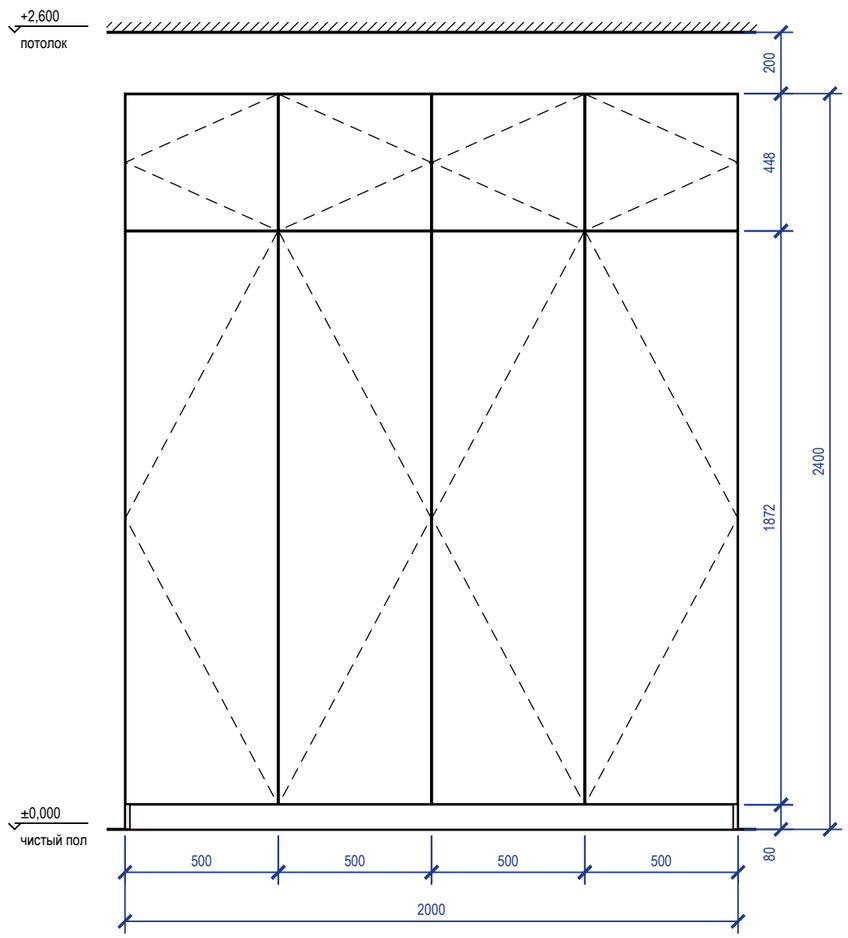


Вид без фасадов (М 1:20)

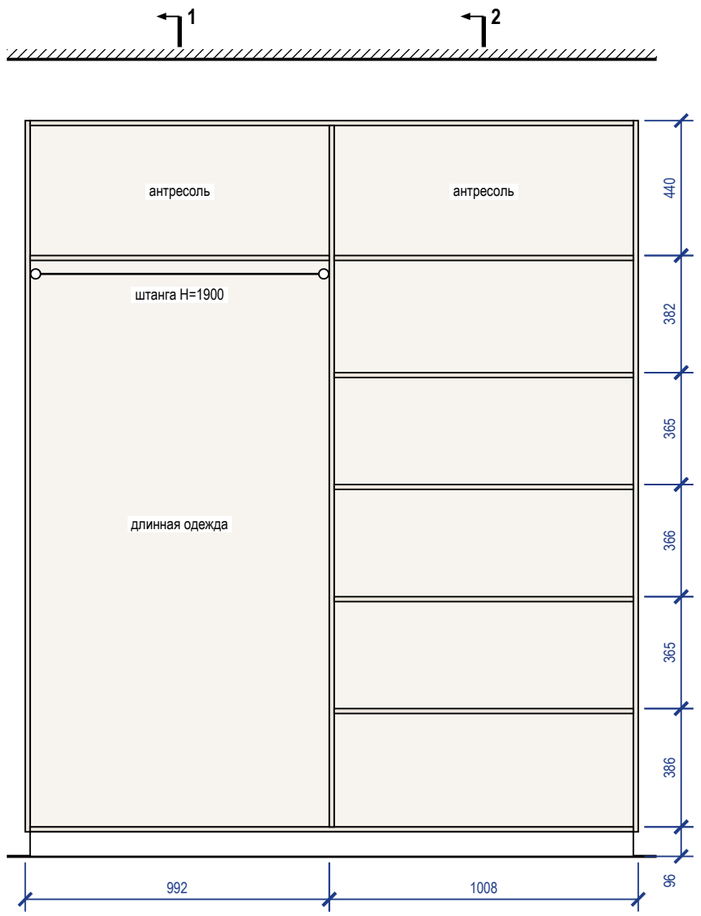

Разрез 1-1 (М 1:20)

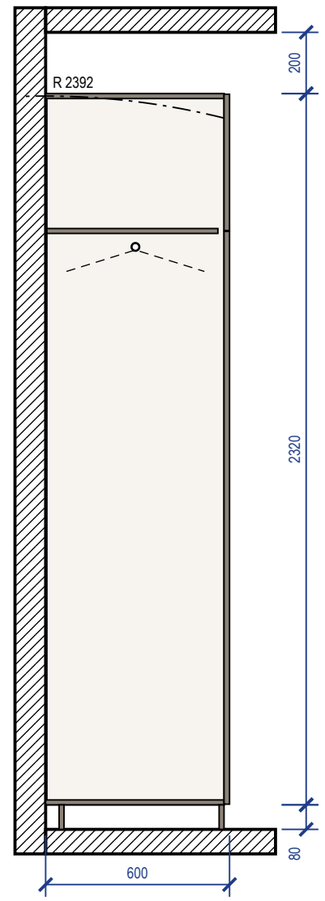


Разрез 2-2 (М 1:20)

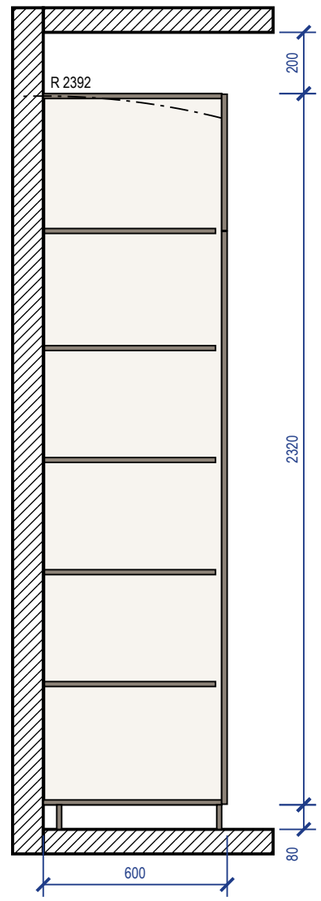

Примечания

1. Размеры — в мм по чистовой отделке; изделие 2000×600×2400 (Ш×Г×В). Перед раскроем — контрольный замер цеха после чистовой отделки стен, пола и потолка.
2. Корпус — ЛДСП 16 мм, задняя стенка ХДФ 4 мм в паз, цоколь 80 мм на регулируемых опорах; фасады накладные — МДФ 18 мм, эмаль матовая, 18 мм; цвет — по колерной карте; петли с доводчиком: фасад 1869 мм — 4 петли, фасад 445 мм — 2 петли.
3. Кромка: скрытые торцы 0,4 мм, видимые 2 мм (ПВХ/АБС).
4. Номинальные зазоры: между фасадами 3 мм, фасад — стена и фасад — потолок не менее 3 мм, фасад ящика — стойка 2 мм.
5. Присадка по 32-й системе — выполняет цех.
6. Зазор до потолка 200 мм.
7. Подъём корпуса: диагональ боковины без цоколя $\sqrt{(2320^2 + 582^2)} = 2392$ мм < 2600 мм до потолка — корпус собирается лёжа, поднимается поворотом и ставится на цоколь.
8. Крепление к стене от опрокидывания: уголок к стене, 3 шт.; основание стены и шаг анкеров — монтажная схема шкафов.


3D орто

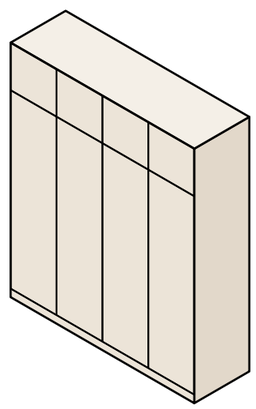


	Лист	№ док.	Подпись	Дата	Проект: Четырёхкомнатная квартира			М 1:20
Дизайнер	Кырлан А.С.			14.11.26	Шкаф распашной М-36	Стадия	Лист	Листов
Проверил						П	Д10	147
Н. контр.								
Утв.								

выпуск 14.11.2026 № e7147312ff · стр. 122 из 147


Общий вид (М 1:25)

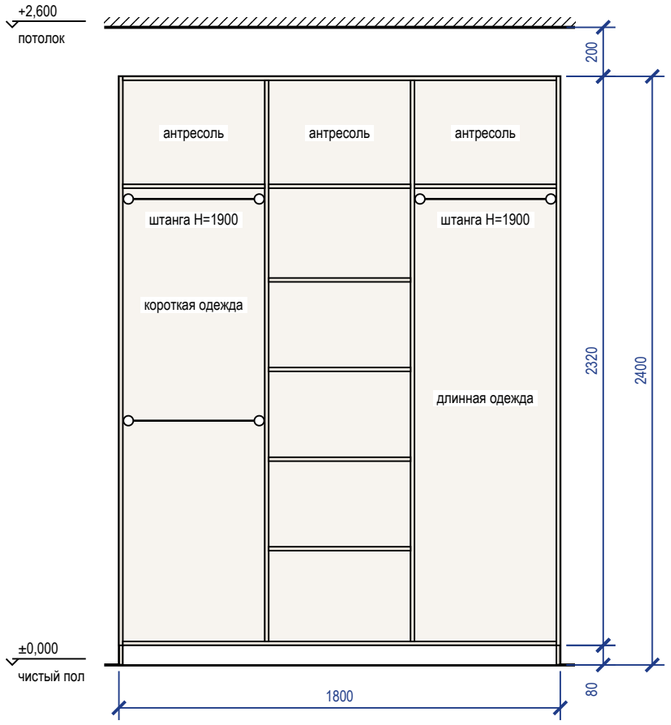


Наполнение, размеры в свету (М 1:25)

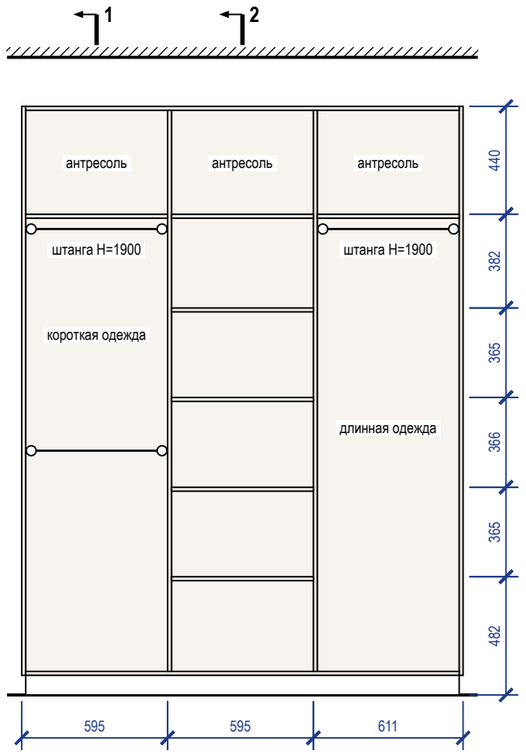

Разрез 1-1 (М 1:25)

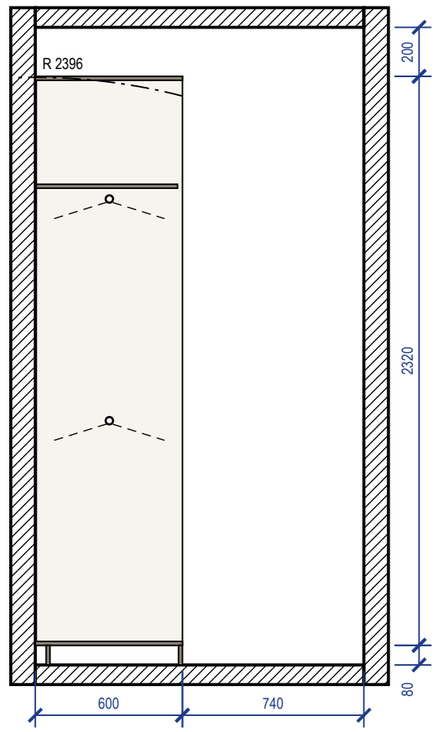


Разрез 2-2 (М 1:25)

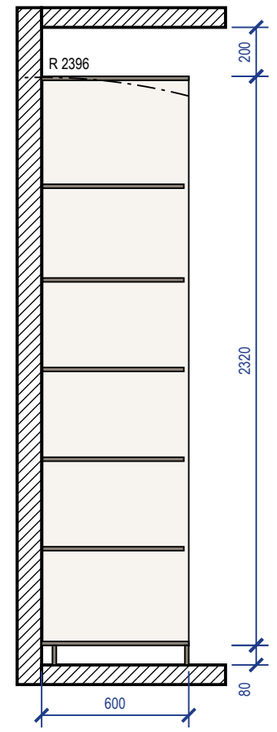

Примечания

1. Размеры — в мм по чистовой отделке; изделие 1800×600×2400 (Ш×Г×В). Перед раскроем — контрольный замер цеха после чистовой отделки стен, пола и потолка.
2. Корпус — ЛДСП 16 мм, задняя стенка ХДФ 4 мм в паз, цоколь 80 мм на регулируемых опорах; открытая система: без фасадов.
3. Кромка: скрытые торцы 0,4 мм, видимые 2 мм (ПВХ/АБС).
4. Присадка по 32-й системе — выполняет цех.
5. Зазор до потолка 200 мм.
6. Подъём корпуса: диагональ боковины без цоколя $\sqrt{(2320^2 + 600^2)} = 2396$ мм < 2600 мм до потолка — корпус собирается лёжа, поднимается поворотом и ставится на цоколь.
7. Крепление к стене от опрокидывания: крепление к стене, 4 точки; основание стены и шаг анкеров — монтажная схема шкафов.
8. Проход перед изделием 740 мм показан на разрезе 1-1.


3D орто

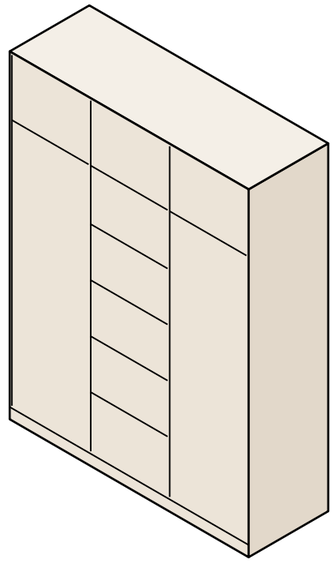


	Лист	№ док.	Подпись	Дата	Проект: Четырёхкомнатная квартира			М 1:25
Дизайнер	Кырлан А.С.			14.11.26	Система хранения М-40	Стадия	Лист	Листов
Проверил						П	Д11	147
Н. контр.								
Утв.								

выпуск 14.11.2026 № e7147312ff · стр. 123 из 147


Общий вид (М 1:20)

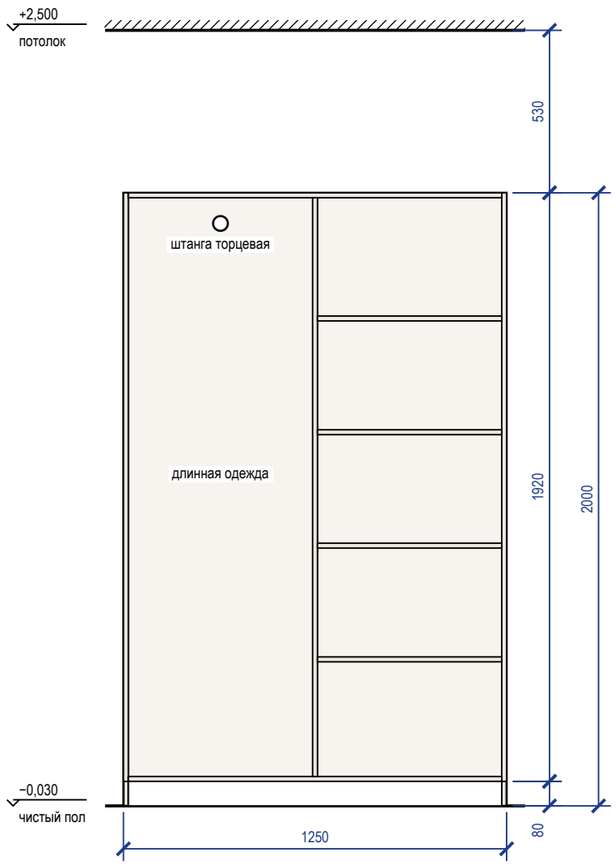


Наполнение, размеры в свету (М 1:20)

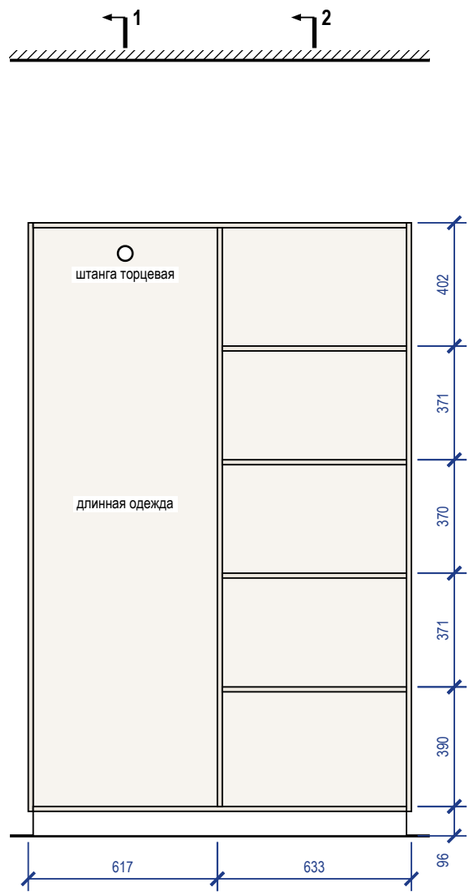

Разрез 1-1 (М 1:20)

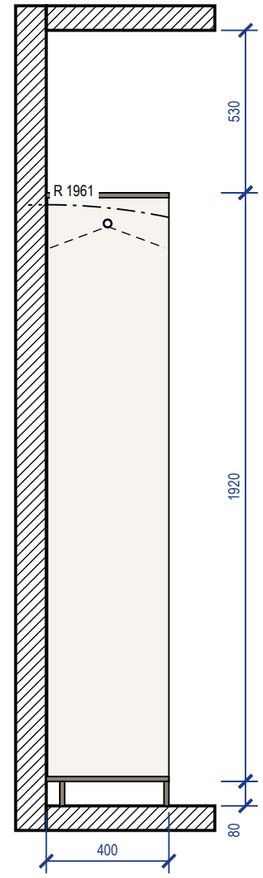


Разрез 2-2 (М 1:20)

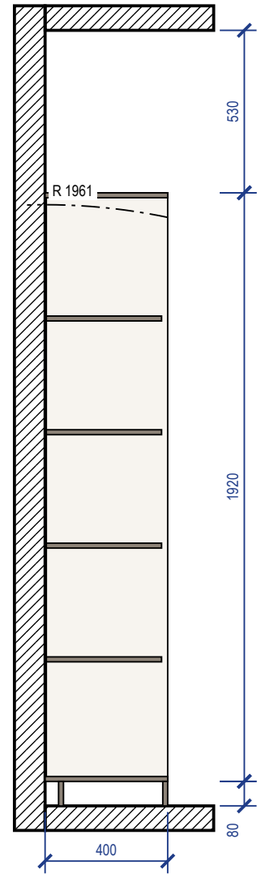

Примечания

1. Размеры — в мм по чистовой отделке; изделие 1250×400×2000 (Ш×Г×В). Перед раскроем — контрольный замер цеха после чистовой отделки стен, пола и потолка.
2. Корпус — ЛДСП 16 мм, задняя стенка ХДФ 4 мм в паз, цоколь 80 мм на регулируемых опорах; открытая система: без фасадов.
3. Кромка: скрытые торцы 0,4 мм, видимые 2 мм (ПВХ/АБС).
4. Присадка по 32-й системе — выполняет цех.
5. Зазор до потолка 530 мм.
6. Подъём корпуса: диагональ боковины без цоколя $\sqrt{(1920^2 + 400^2)} = 1961$ мм < 2530 мм до потолка — корпус собирается лёжа, поднимается поворотом и ставится на цоколь.
7. Крепление к стене от опрокидывания: крепление к стене, 3 точки; основание стены и шаг анкеров — монтажная схема шкафов.


3D орто

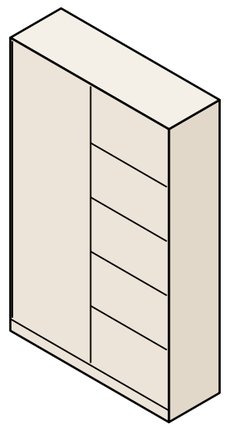


	Лист	№ док.	Подпись	Дата	Проект: Четырёхкомнатная квартира			М 1:20
Дизайнер	Кырлан А.С.			14.11.26	Система хранения М-41	Стадия	Лист	Листов
Проверил						П	Д12	147
Н. контр.								
Утв.								

выпуск 14.11.2026 № e7147312ff · стр. 124 из 147


Общий вид (М 1:20)

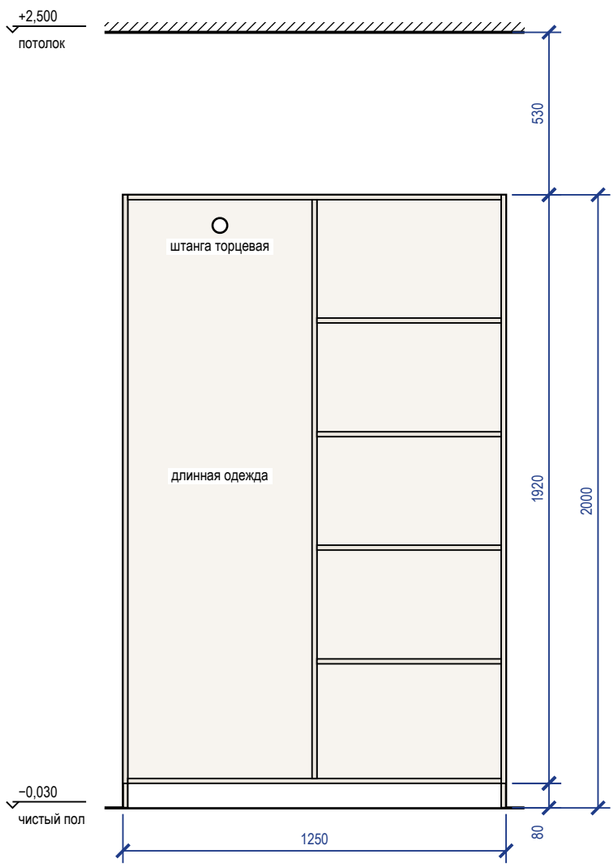


Наполнение, размеры в свету (М 1:20)

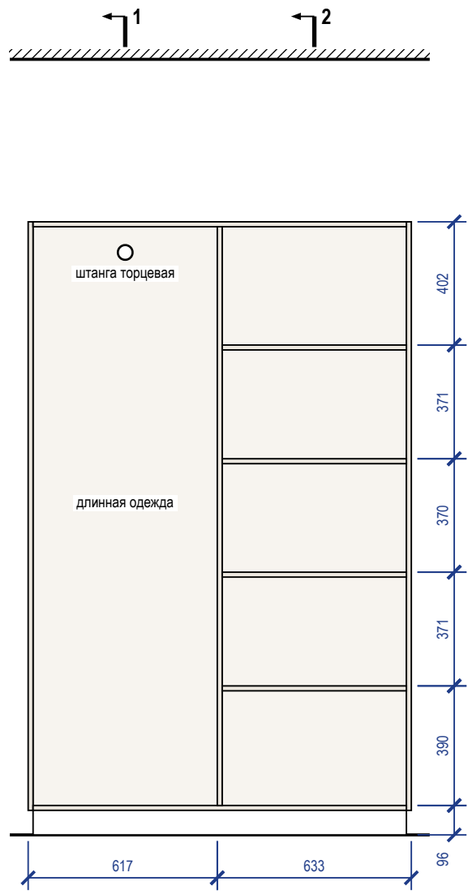

Разрез 1-1 (М 1:20)

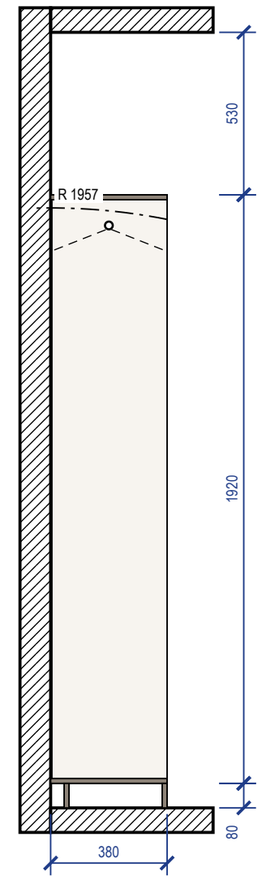


Разрез 2-2 (М 1:20)

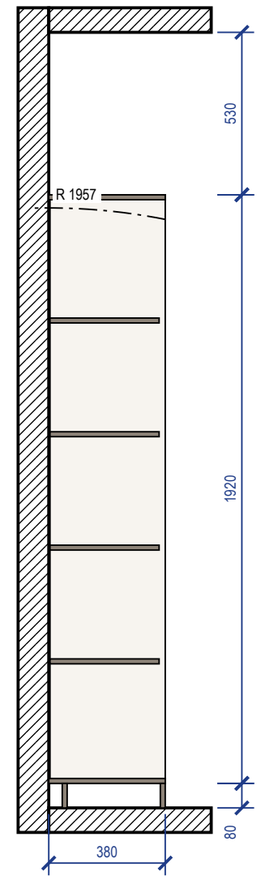

Примечания

1. Размеры — в мм по чистовой отделке; изделие 1250×380×2000 (Ш×Г×В). Перед раскроем — контрольный замер цеха после чистовой отделки стен, пола и потолка.
2. Корпус — ЛДСП 16 мм, задняя стенка ХДФ 4 мм в паз, цоколь 80 мм на регулируемых опорах; открытая система: без фасадов.
3. Кромка: скрытые торцы 0,4 мм, видимые 2 мм (ПВХ/АБС).
4. Присадка по 32-й системе — выполняет цех.
5. Зазор до потолка 530 мм.
6. Подъём корпуса: диагональ боковины без цоколя $\sqrt{(1920^2 + 380^2)} = 1957$ мм < 2530 мм до потолка — корпус собирается лёжа, поднимается поворотом и ставится на цоколь.
7. Крепление к стене от опрокидывания: крепление к стене, 3 точки; основание стены и шаг анкеров — монтажная схема шкафов.


3D орто

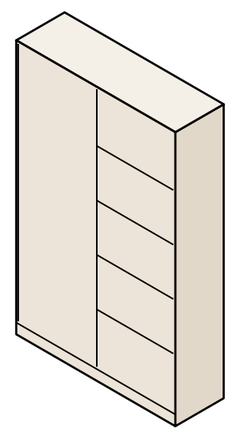


	Лист	№ док.	Подпись	Дата	Проект: Четырёхкомнатная квартира			М 1:20
Дизайнер	Кырлан А.С.			14.11.26	Система хранения М-42	Стадия	Лист	Листов
Проверил						П	Д13	147
Н. контр.								
Утв.								

выпуск 14.11.2026 № e7147312ff · стр. 125 из 147


Вид с фасадами (М 1:25)

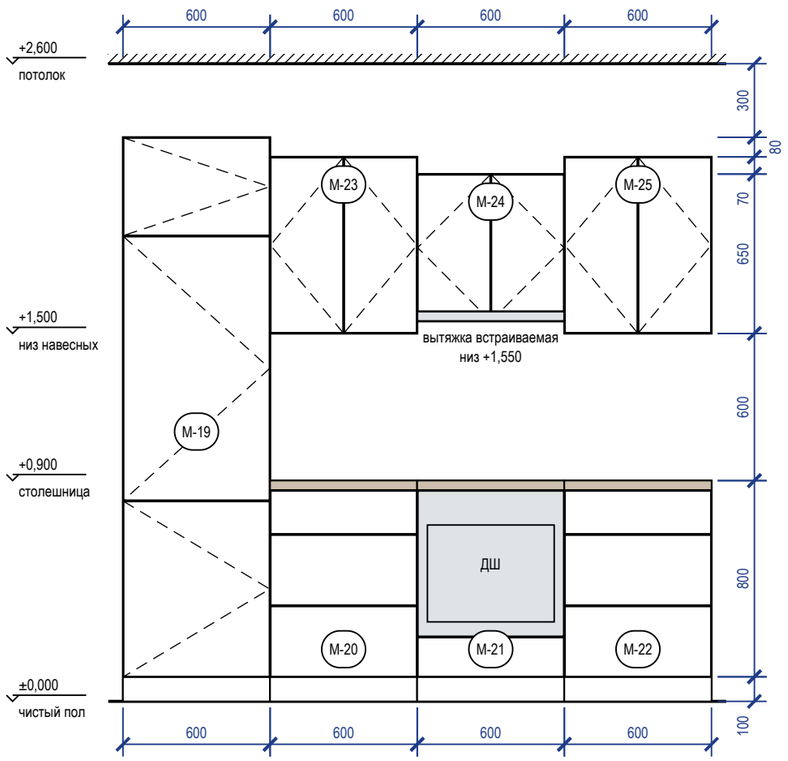


Вид без фасадов: наполнение, выводы (М 1:25)

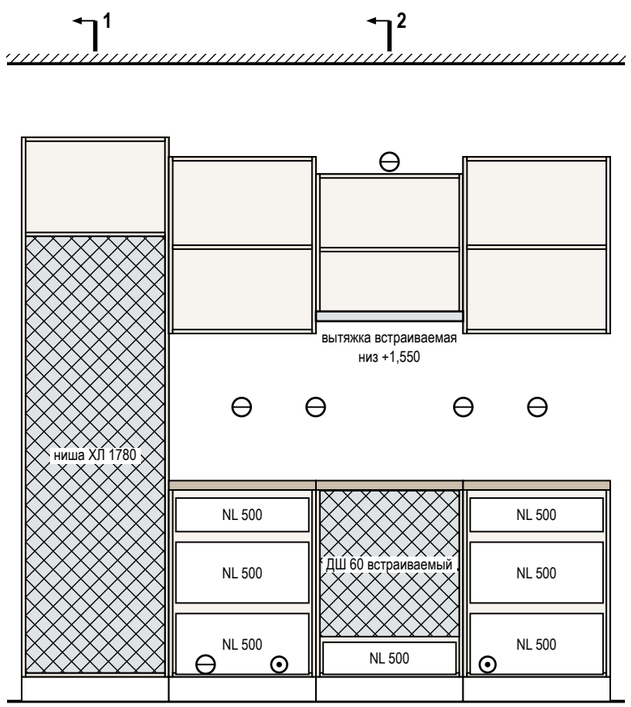


Разрез 1-1 (М 1:25)

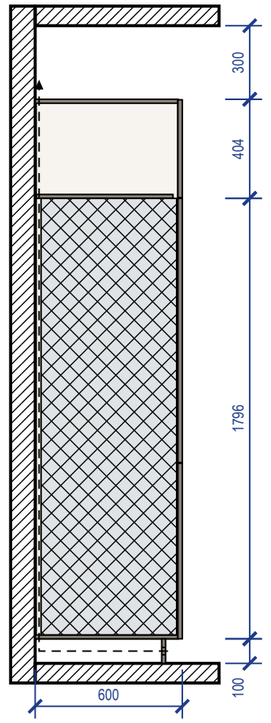

Разрез 2-2 (М 1:25)

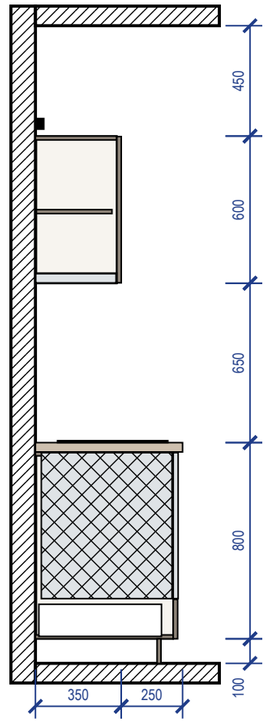

3D орто

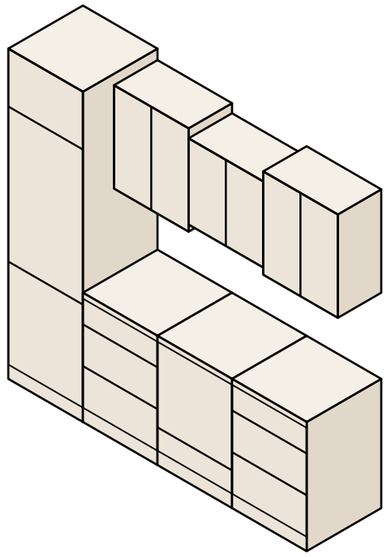


Примечания

1. Размеры — в мм по чистовой отделке, вид из помещения; марки — как на плане расстановки. Перед раскроем — контрольный замер цеха после фартука и пола.
2. Корпуса — ЛДСП 16 мм, задняя стенка ХДФ 4 мм; фасады — МДФ, эмаль матовая 18 мм, цвет по колерной карте; столешница 38 мм, свес 20 мм; цоколь 100 мм.
3. Кромка: скрытые торцы 0,4 мм, видимые 2 мм. Номинальные зазоры: между фасадами 3 мм, фасад — столешница 3 мм, фасад — стена не менее 3 мм.
4. Ящики полного выдвижения и петли — с доводчиком; присадка по 32-й системе — выполняет цех.
5. Наименования и габариты модулей (М…) — в ведомости изделий, лист 38.
6. Вытяжка встраивается в дно навесного модуля М-24 над варочной: её низ на 1550 мм от пола, 650 мм над панелью (не меньше 650 мм).
7. Ниши техники (холодильник — ориентир 1780 мм) — по монтажным схемам выбранных моделей: решётка в цоколе и канал за пеналом холодильника, зазор за духовым шкафом, фасад ПММ на двери машины.


	Лист	№ док.	Подпись	Дата	Проект: Четырёхкомнатная квартира			М 1:25
Дизайнер	Кырлан А.С.			14.11.26	Кухня (пом. 6). Развёртка гарнитура	Стадия	Лист	Листов
Проверил						П	Д14	147
Н. контр.								
Утв.								

выпуск 14.11.2026 № e7147312ff · стр. 126 из 147


Вид с фасадами (М 1:20)

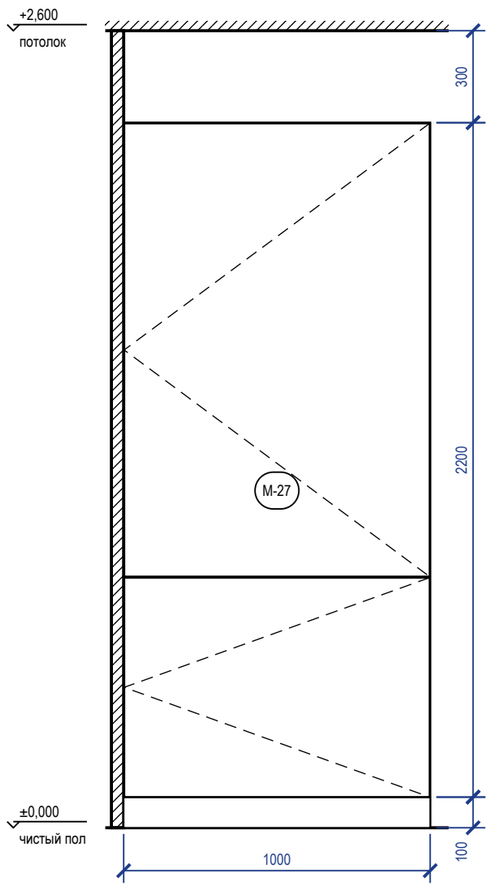


Вид без фасадов: наполнение, выводы (М 1:20)

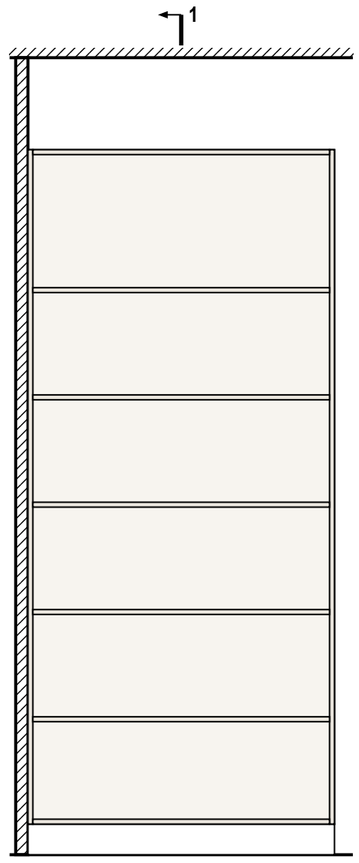

Разрез 1-1 (М 1:20)

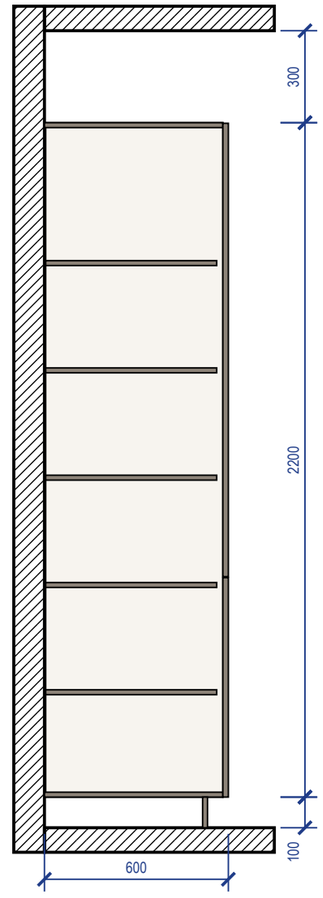

3D орто

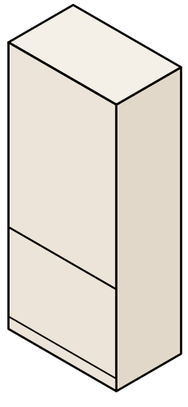


Примечания

1. Размеры — в мм по чистовой отделке, вид из помещения; марки — как на плане расстановки. Перед раскроем — контрольный замер цеха после фартука и пола.
2. Корпуса — ЛДСП 16 мм, задняя стенка ХДФ 4 мм; фасады — МДФ, эмаль матовая 18 мм, цвет по колерной карте; столешница 38 мм, свес 20 мм; цоколь 100 мм.
3. Кромка: скрытые торцы 0,4 мм, видимые 2 мм. Номинальные зазоры: между фасадами 3 мм, фасад — столешница 3 мм, фасад — стена не менее 3 мм.
4. Ящики полного выдвижения и петли — с доводчиком; присадка по 32-й системе — выполняет цех.
5. Наименования и габариты модулей (М…) — в ведомости изделий, лист 38.
6. Ниши техники — по монтажным схемам выбранных моделей: решётка в цоколе и канал за пеналом холодильника, зазор за духовым шкафом, фасад ПММ на двери машины.

	Лист	№ док.	Подпись	Дата	Проект: Четырёхкомнатная квартира			М 1:20
Дизайнер	Кырлан А.С.			14.11.26				
Проверил					Кухня (пом. 6). Развёртка гарнитура	Стадия	Лист	Листов
Н. контр.								
Утв.						П	Д15	147


выпуск 14.11.2026 № e7147312ff · стр. 127 из 147

План (вид сверху) (М 1:25)

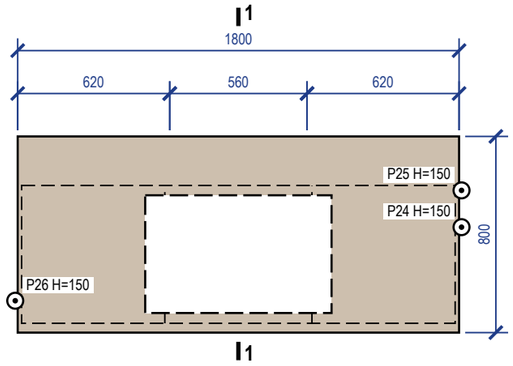


▲ рабочая сторона — северная (к стене А), проход 1200


Вид с рабочей стороны (М 1:25)

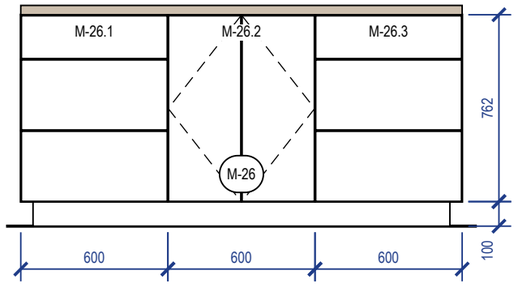


Вид без фасадов: наполнение, вывод (М 1:25)

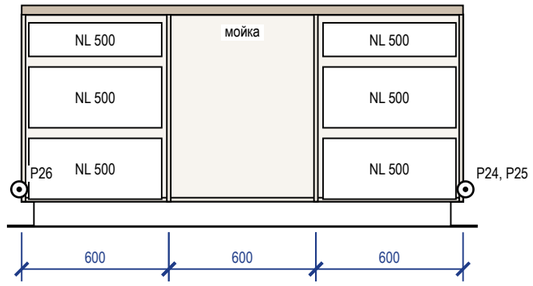

Разрез 1-1 (М 1:25)

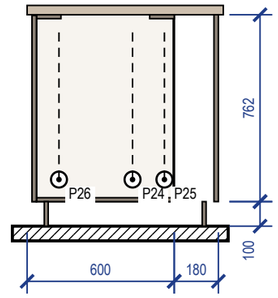

3D орто

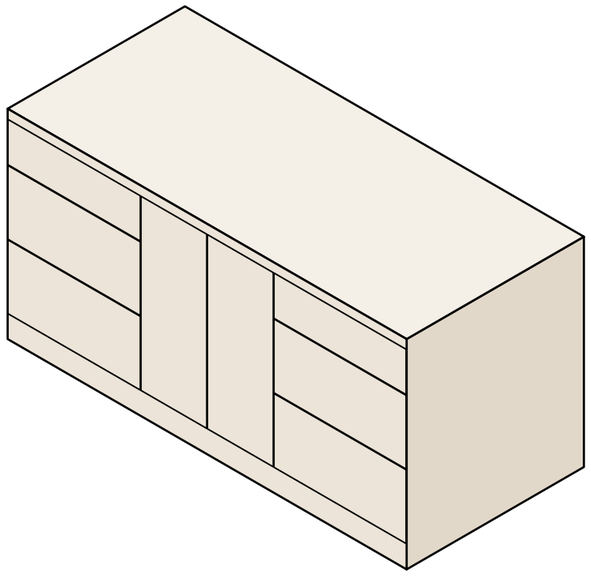

Примечания

1. Размеры — в мм по чистовому полу; перед раскроем — контрольный замер цеха после укладки пола. Остров крепится к полу (уголки в цоколе), выравнивается опорами ±20 мм.
2. Корпуса — ЛДСП 16 мм, задняя стенка ХДФ 4 мм; фасады — МДФ, эмаль матовая 18 мм; столешница 38 мм, свес 20 мм по периметру; цоколь 100 мм с отступом 50 мм.
3. Кромка: скрытые торцы 0,4 мм, видимые 2 мм. Номинальные зазоры: между фасадами 3 мм, фасад — столешница 3 мм.
4. Рабочая сторона — северная (к стене А): проход 1200 мм; с тыла — глухая панель. Членение и сторона — предложение мебельщика.
5. Питание: P24 — торцевая панель острова M-26: мелкая техника, H=150; P25 — торцевая панель острова M-26: мелкая техника, H=150; P26 — посудомоечная машина в острове M-26, H=150; кабель — внутри модуля до панели, доступ через съёмный цоколь.

Спецификация изделия M-26

Поз.	Наименование	Тип, размер	Кол.
M-26.1	модуль с ящиками	600×800×900	1
M-26.2	модуль под мойку	600×800×900	1
M-26.3	модуль с ящиками	600×800×900	1
M-26.2	Мойка врезная / подстольная с сифоном	вырез по шаблону, ориентир 760 × 480	1
	Направляющие полного выдвижения с доводчиком NL 500	пара	6
	Ручка-профиль	латунь матовая	8
	Петля накладная 110° с доводчиком	чашка 35 мм	4
	Опора кухонная регулируемая 100–120 мм	+ клипса цоколя	12
	Уголок крепления острова к полу	стальной, в цоколе	4

	Лист	№ док.	Подпись	Дата
Дизайнер	Кырлан А.С.			14.11.26
Проверил				
Н. контр.				
Утв.				

Проект: Четырёхкомнатная квартира — **М 1:25**

Остров M-26 (пом. 6). Чертёж изделия

Стадия	Лист	Листов
П	Д16	147

Ведомость отделки помещений (форма 1 прил. А ГОСТ 21.501-2018). Лист 1 из 2

№	Наименование помещения	Потолок			Стены и перегородки			Низ стен (плинтус)			Пол		Примечание
		Вид отделки	Код цвета	S, м²	Вид отделки	Код цвета	S, м²	Вид отделки	Код цвета	L, м	Вид отделки	S, м²	
1	Зал 18,16 м²	ГКЛ по каркасу П113, отм. +2,500; +2,600; окраска, Tikkurila Anti-Reflex 2, глубокоматовая, 2 слоя, подготовка Q3	Tikkurila F497	18,16	Окраска, Tikkurila Optiva 5 Matt, матовая, 2 слоя, подготовка К3 Акцент — стена А: окраска, Tikkurila Optiva 5 Matt, матовая, 3 слоя, аналог: интерьерная краска, класс 2 по EN 13300, глубокоматовая/матовая, база С, подготовка К3	Tikkurila F497 Tikkurila L481	25,94 13,55	Плинтус МДФ h=80 мм, аналог: МДФ под окраску 80×16 мм	Tikkurila F497	16,6	Инженерная доска, аналог: дуб натуральный брашированный, масло-воск, 14/4 мм, на клею; тип 1, отм. ЧП ±0,000	18,16	Н стен 2500 (до потолка); плинтус в цвет: стены
2	Ванная комната 5,57 м²	ГКЛВ по каркасу П113, отм. +2,500; окраска, Tikkurila Luja 7, матовая, 2 слоя, подготовка Q3	Tikkurila F497	5,57	Облицовка плиткой, аналог: керамогранит матовый, тон F497, 600×600×9 мм, клей С2 TE S1, затирка CG2WA	#F1F1EC	22,35	нет (облицовка от пола)			Аналог: керамогранит матовый R10, тон J484, 600×600×10 мм; тип 2, отм. ЧП −0,015	5,57	Н стен 2515 (до потолка); тёплый пол; гидроизоляция обмазочная, 2 слоя, по всему помещению, с заведением на стены 200 мм; над ванной — до 2100 и 300 мм за борт (по пирогу пола); тест проливом и акт скрытых работ; облицовка от чистого пола до низа потолка
3	Тёмная комната 2,96 м²	ГКЛ по каркасу П113, отм. +2,600; окраска, Tikkurila Anti-Reflex 2, глубокоматовая, 2 слоя, подготовка Q3	Tikkurila F497	2,96	Окраска, Tikkurila Optiva 5 Matt, матовая, 2 слоя, подготовка К3	Tikkurila F497	16,94	Плинтус МДФ h=80 мм, аналог: МДФ под окраску 80×16 мм	Tikkurila F497	6,4	Инженерная доска, аналог: дуб натуральный брашированный, масло-воск, 14/4 мм, на клею; тип 1, отм. ЧП ±0,000	2,96	Н стен 2600 (до потолка); плинтус в цвет: стены
4	Детская 1 17,51 м²	ГКЛ по каркасу П113, отм. +2,600; окраска, Tikkurila Anti-Reflex 2, глубокоматовая, 2 слоя, подготовка Q3	Tikkurila F497	17,51	Окраска, Tikkurila Joker, полуматовая, 2 слоя, подготовка К3	Tikkurila F497	40,12	Плинтус МДФ h=80 мм, аналог: МДФ под окраску 80×16 мм	Tikkurila F497	16,2	Инженерная доска, аналог: дуб натуральный брашированный, масло-воск, 14/4 мм, на клею; тип 1, отм. ЧП ±0,000	17,51	Н стен 2600 (до потолка); плинтус в цвет: стены
5	Коридор 4,54 м²	ГКЛ по каркасу П113, отм. +2,600; окраска, Tikkurila Anti-Reflex 2, глубокоматовая, 2 слоя, подготовка Q3	Tikkurila F497	4,54	Окраска, Tikkurila Optiva 20 Semimatt, полуматовая, 2 слоя, подготовка К3	Tikkurila J484	22,21	Плинтус МДФ h=80 мм, аналог: МДФ под окраску 80×16 мм	Tikkurila J484	8,1	Аналог: керамогранит матовый R10, тон V486, 600×600×10 мм; тип 3, отм. ЧП ±0,000	4,54	Н стен 2600 (до потолка); плинтус в цвет: стены
6	Кухня 15,19 м²	ГКЛ по каркасу П113, отм. +2,600; окраска, Tikkurila Luja 7, матовая, 2 слоя, подготовка Q3	Tikkurila F497	15,19	Окраска, Tikkurila Luja 7, полуматовая, 2 слоя, подготовка К3 Фартук кухни (стена А): облицовка керамогранитом, аналог: керамогранит матовый, тон F497, 600×600×9 мм, клей С2 TE S1, затирка CG2WA	Tikkurila F497 #F1F1EC	34,48 1,11	Плинтус МДФ h=80 мм, аналог: МДФ под окраску 80×16 мм	Tikkurila F497	13,8	Инженерная доска, аналог: дуб натуральный брашированный, масло-воск, 14/4 мм, на клею; тип 4, отм. ЧП ±0,000	15,19	Н стен 2600 (до потолка); гидроизоляция обмазочная, 2 слоя, с заведением на стены 200 мм (по пирогу пола); тест проливом и акт скрытых работ; влагостойкая полуматовая окраска (класс мокрого истирания 1 по EN 13300); категория К3 по СП 71.13330.2017, табл. 7.5; по ГКЛ каркаса П113, влагостойкая окраска; Q3 плинтус в цвет: стены
7	Прихожая-коридор 7,80 м²	ГКЛ по каркасу П113, отм. +2,600; окраска, Tikkurila Anti-Reflex 2, глубокоматовая, 2 слоя, подготовка Q3	Tikkurila F497	7,80	Окраска, Tikkurila Optiva 20 Semimatt, полуматовая, 2 слоя, подготовка К3	Tikkurila J484	23,80	Плинтус МДФ h=80 мм, аналог: МДФ под окраску 80×16 мм	Tikkurila J484	8,7	Аналог: керамогранит матовый R10, тон V486, 600×600×10 мм; тип 3, отм. ЧП ±0,000	7,80	Н стен 2600 (до потолка); плинтус в цвет: стены
8	Гардеробная 2 1,29 м²	ГКЛ по каркасу П113, отм. +2,600; окраска, Tikkurila Anti-Reflex 2, глубокоматовая, 2 слоя, подготовка Q3	Tikkurila F497	1,29	Окраска, Tikkurila Optiva 5 Matt, матовая, 2 слоя, подготовка К3	Tikkurila F497	8,65	Плинтус МДФ h=80 мм, аналог: МДФ под окраску 80×16 мм	Tikkurila F497	3,3	Инженерная доска, аналог: дуб натуральный брашированный, масло-воск, 14/4 мм, на клею; тип 1, отм. ЧП ±0,000	1,29	Н стен 2600 (до потолка); плинтус в цвет: стены
9	Детская 2 10,96 м²	ГКЛ по каркасу П113, отм. +2,600; окраска, Tikkurila Anti-Reflex 2, глубокоматовая, 2 слоя, подготовка Q3	Tikkurila F497	10,96	Окраска, Tikkurila Joker, полуматовая, 2 слоя, подготовка К3	Tikkurila F497	29,08	Плинтус МДФ h=80 мм, аналог: МДФ под окраску 80×16 мм	Tikkurila F497	11,8	Инженерная доска, аналог: дуб натуральный брашированный, масло-воск, 14/4 мм, на клею; тип 1, отм. ЧП ±0,000	10,96	Н стен 2600 (до потолка); плинтус в цвет: стены

Примечания

1. Ведомость продолжена на листе 2 из 2; итоги, сводка площадей и примечания — на последнем листе ведомости.

	Лист	№ док.	Подпись	Дата	Проект: Четырёхкомнатная квартира			
Дизайнер	Кырлан А.С.			14.11.26	Ведомость отделки помещений. Лист 1 из 2	Стадия	Лист	Листов
Проверил						П	С1	147
Н. контр.								
Утв.								

выпуск 14.11.2026 № e7147312ff · стр. 129 из 147

Ведомость отделки помещений (форма 1 прил. А ГОСТ 21.501-2018). Лист 2 из 2

№	Наименование помещения	Потолок			Стены и перегородки			Низ стен (плинтус)			Пол		Примечание
		Вид отделки	Код цвета	S, м²	Вид отделки	Код цвета	S, м²	Вид отделки	Код цвета	L, м	Вид отделки	S, м²	
10	Санузел 1,31 м²	ГКЛВ по каркасу П113, отм. +2,500; окраска, Tikkurila Luja 7, матовая, 2 слоя, подготовка Q3	Tikkurila F497	1,31	Облицовка плиткой, аналог: керамогранит матовый, тон F497, 600×600×9 мм, клей C2 TE S1, затирка CG2WA	#F1F1EC	10,46	нет (облицовка от пола)			Аналог: керамогранит матовый R10, тон J484, 600×600×10 мм; тип 2, отм. ЧП −0,015	1,31	Н стен 2515 (до потолка); тёплый пол; гидроизоляция обмазочная, 2 слоя, по всему помещению, с заведением на стены 200 мм (по пирогу пола); тест проливом и акт скрытых работ; облицовка от чистого пола до низа потолка
11	Гостиная 14,55 м²	ГКЛ по каркасу П113, отм. +2,600; окраска, Tikkurila Anti-Reflex 2, глубокоматовая, 2 слоя, подготовка Q3	Tikkurila F497	14,55	Окраска, Tikkurila Optiva 5 Matt, матовая, 2 слоя, подготовка К3 Акцент — стена А: окраска, Tikkurila Optiva 5 Matt, матовая, 3 слоя, аналог: интерьерная краска, класс 2 по EN 13300, глубокоматовая/матовая, база С, подготовка К3	Tikkurila F497 Tikkurila L481	27,79 11,13	Плинтус МДФ h=80 мм, аналог: МДФ под окраску 80×16 мм	Tikkurila F497	15,6	Инженерная доска, аналог: дуб натуральный брашированный, масло-воск, 14/4 мм, на клею; тип 1, отм. ЧП ±0,000	14,55	Н стен 2600 (до потолка); плинтус в цвет: стены
12	Гардеробная 1 2,83 м²	ГКЛ по каркасу П113, отм. +2,600; окраска, Tikkurila Anti-Reflex 2, глубокоматовая, 2 слоя, подготовка Q3	Tikkurila F497	2,83	Окраска, Tikkurila Optiva 5 Matt, матовая, 2 слоя, подготовка К3	Tikkurila F497	14,96	Плинтус МДФ h=80 мм, аналог: МДФ под окраску 80×16 мм	Tikkurila F497	5,5	Инженерная доска, аналог: дуб натуральный брашированный, масло-воск, 14/4 мм, на клею; тип 1, отм. ЧП ±0,000	2,83	Н стен 2600 (до потолка); плинтус в цвет: стены
13	Балкон 1 3,70 м²	ГКЛВ по каркасу П113, отм. +2,500; окраска, Tikkurila Luja 7, матовая, 2 слоя, подготовка Q3	Tikkurila F497	3,70	Окраска, Tikkurila Luja 7, полуматовая, 2 слоя, подготовка К3	Tikkurila F497	16,51	Плинтус из керамогранита h=80 мм, аналог: из керамогранита пола, подрезка 80 мм, верхняя кромка с запилом 45°	#B8AFA5	7,7	Аналог: керамогранит матовый R11, тон V486, 600×600×10 мм; тип 5, отм. ЧП −0,030	3,70	Н стен 2530 (до потолка); влагостойкая окраска по утеплённой стене; категория К3 по СП 71.13330.2017, табл. 7.5
	Итого			**106,37**			**319,07**			**113,7**		**106,37**	

Сводка площадей по материалам отделки

Поверхность	Материал / код цвета	Серия	Площадь, м²
Потолок	Tikkurila F497	Anti-Reflex 2	80,60
Потолок	Tikkurila F497	Luja 7	25,77
Стены	Tikkurila F497	Optiva 5 Matt	94,28
Стены	Tikkurila L481	Optiva 5 Matt	24,68
Стены	облицовка плиткой 600×600×9 мм, #F1F1EC	аналог: керамогранит матовый, тон F497	32,81
Стены	Tikkurila F497	Joker	69,20
Стены	Tikkurila J484	Optiva 20 Semimatt	46,01
Стены	Tikkurila F497	Luja 7	50,99
Фартук	облицовка керамогранитом 600×600×9 мм, #F1F1EC	аналог: керамогранит матовый, тон F497	1,11

Примечания

1. Площади поверхностей — по чистым граням стен до отделки: стены = периметр × высоту от чистого пола помещения до низа потолка минус проёмы (облицовка плиткой — до верха облицовки); плинтус = периметр минус дверные проёмы; пол и потолок — по площади помещения. Количество плиток по раскладке. Площади помещений — с учётом всех частей помещения; откосы в площадь стен не входят.
2. Акцентные стены и фартук — отдельными строками, их площадь вычтена из основной отделки стен помещения; фартук — над нижними модулями кухни от столешницы до низа навесных шкафов, где шкафов нет — на 600 мм.
3. Плинтус — длина по периметру за вычетом дверных проёмов; примыкания к наличникам и встроенной мебели — по развёрткам.
4. Формат плитки — Ш×В×Т (ширина × высота в положении укладки × толщина), мм; на полу — вдоль стен А/В × вдоль стен Б/Г.
5. Коды цвета — по веерам производителей; колеровка каждой краски одной партией, проверка выкраса при свете D65 и при лампах проекта.
6. Уровни подготовки Q1–Q4 — система Knauf, не норма ГОСТ/СП; допуски поверхностей — по СП 71.13330.2017 (действующая редакция).
7. «аналог:» — изделие задано характеристиками, марку и артикул согласовать с заказчиком до закупки.
8. Плавающая стяжка по звукоизоляции: демпферная (кромочная) лента по контуру помещения и у стояков (СП 51.13330.2011, п. 9.11); плинтус крепится только к стене.
9. Помещения 1, 3, 4, 5, 6, 7, 8, 9, 11, 12: колеруется в код стен, но по эмали на МДФ: сличать отдельным выкрасом на своей подложке (выкрас № 10).
10. Помещения 2, 10, 13: по ГКЛВ каркаса П113, влагостойкая окраска; Q3.

	Лист	№ док.	Подпись	Дата	Проект: Четырёхкомнатная квартира			
Дизайнер	Кырлан А.С.			14.11.26	Ведомость отделки помещений. Лист 2 из 2	Стадия	Лист	Листов
Проверил						П	С2	147
Н. контр.								
Утв.								

выпуск 14.11.2026 № e7147312ff · стр. 130 из 147

Поз.	Наименование и техническая характеристика	Тип, марка, обозначение документа	Код продукции	Поставщик	Ед. изм.	Кол.	Образец	Примечание
	Лакокрасочные материалы							
1	Краска интерьерная водно-дисперсионная акриловая для стен, матовая, класс мокрого истирания 2 по EN 13300, база A; цвет по вееру Tikkurila F497 «Paper», колеровка машинная	Tikkurila Optiva 5 Matt		Tikkurila	л	26,1		поз. К1 колерной карты; пом. 1, 3, 8, 11, 12; S = 94,3 м² × 2 сл. × 0,12 л/м² = 22,6 л, +10 % и 0,5 л на подкраску → ≥ 25,4 л; тара 2 × 9 л + 3 × 2,7 л
2	Краска интерьерная водно-дисперсионная акриловая для акцентных стен, матовая, класс мокрого истирания 2 по EN 13300, база C; цвет по вееру Tikkurila L481 «Silhouette», колеровка машинная	Tikkurila Optiva 5 Matt		Tikkurila	л	10,8		поз. К2 колерной карты; пом. 1, 11; S = 24,7 м² × 3 сл. × 0,12 л/м² = 8,9 л, +10 % и 0,5 л на подкраску → ≥ 10,3 л; тара 1 × 9 л + 2 × 0,9 л
3	Краска интерьерная водно-дисперсионная акриловая для потолков, глубокоматовая, класс мокрого истирания 2 по EN 13300, база A; цвет по вееру Tikkurila F497 «Paper», колеровка машинная	Tikkurila Anti-Reflex 2		Tikkurila	л	22,5		поз. К3 колерной карты; пом. 1, 3, 4, 5, 7, 8, 9, 11, 12; S = 80,6 м² × 2 сл. × 0,12 л/м² = 19,3 л, +10 % и 0,5 л на подкраску → ≥ 21,8 л; тара 2 × 9 л + 1 × 2,7 л + 2 × 0,9 л
4	Краска интерьерная водно-дисперсионная акриловая для потолков, матовая, класс мокрого истирания 1 по EN 13300, база A; цвет по вееру Tikkurila F497 «Paper», колеровка машинная	Tikkurila Luja 7		Tikkurila	л	8,1		поз. К5 колерной карты; пом. 2, 6, 10, 13; S = 25,8 м² × 2 сл. × 0,12 л/м² = 6,2 л, +10 % и 0,5 л на подкраску → ≥ 7,3 л; тара 3 × 2,7 л
5	Краска интерьерная водно-дисперсионная акриловая для стен, полуматовая, класс мокрого истирания 2 по EN 13300, база A; цвет по вееру Tikkurila F497 «Paper», колеровка машинная	Tikkurila Joker		Tikkurila	л	18,9		поз. К6 колерной карты; пом. 4, 9; S = 69,2 м² × 2 сл. × 0,12 л/м² = 16,6 л, +10 % и 0,5 л на подкраску → ≥ 18,8 л; тара 2 × 9 л + 1 × 0,9 л
6	Краска интерьерная водно-дисперсионная акриловая для стен, полуматовая, класс мокрого истирания 2 по EN 13300, база A; цвет по вееру Tikkurila J484 «Castle», колеровка машинная	Tikkurila Optiva 20 Semimatt		Tikkurila	л	13,5		поз. К7 колерной карты; пом. 5, 7; S = 46,0 м² × 2 сл. × 0,12 л/м² = 11,0 л, +10 % и 0,5 л на подкраску → ≥ 12,6 л; тара 1 × 9 л + 1 × 2,7 л + 2 × 0,9 л
7	Краска интерьерная водно-дисперсионная акриловая для стен, полуматовая, класс мокрого истирания 1 по EN 13300, база A; цвет по вееру Tikkurila F497 «Paper», колеровка машинная	Tikkurila Luja 7		Tikkurila	л	14,4		поз. К9 колерной карты; пом. 6, 13; S = 51,0 м² × 2 сл. × 0,12 л/м² = 12,2 л, +10 % и 0,5 л на подкраску → ≥ 14,0 л; тара 1 × 9 л + 2 × 2,7 л
8	Акрилово-уретановая эмаль на водной основе, полуглянцевая в цвет Tikkurila F497 «Paper» — окраска плинтуса	аналог по характеристикам			л	2,3		поз. К4; пом. 1, 3, 4, 6, 8, 9, 11, 12; L = 89,2 м, S = 8,6 м² × 2 сл. × 0,12 л/м² + 10 %; продукт подобрать в веере Tikkurila
9	Акрилово-уретановая эмаль на водной основе, полуглянцевая в цвет Tikkurila J484 «Castle» — окраска плинтуса	аналог по характеристикам			л	0,5		поз. К8; пом. 5, 7; L = 16,8 м, S = 1,6 м² × 2 сл. × 0,12 л/м² + 10 %; продукт подобрать в веере Tikkurila
10	Грунтовка акриловая под окраску стен и потолков — из системы производителя краски	по системе краски			м²	392		площадь окраски стен, акцентов и потолков; 1 слой перед окраской; расход — по ТУ грунтовки

	Лист	№ док.	Подпись	Дата	Проект: Четырёхкомнатная квартира			
Дизайнер	Кырлан А.С.			14.11.26				
Проверил					Спецификация отделочных материалов	Стадия	Лист	Листов
Н. контр.						П	С3	147
Утв.								

Поз.	Наименование и техническая характеристика	Тип, марка, обозначение документа	Код продукции	Поставщик	Ед. изм.	Кол.	Образец	Примечание
	Плитка и керамогранит							
11	Керамогранит матовый R10, тон J484, 600.8×600.8 мм	аналог по характеристикам			м²	10,47		шов 2 мм; Ванная комната, пол; Санузел, пол; по раскладке 26 шт (S = 6,88 м²), с запасом 29 шт
12	Керамогранит матовый, тон F497, 600.8×600.8 мм	аналог по характеристикам			м²	63,17		шов 2 мм; Ванная комната, стены А–Г; Ванная комната, короб инсталляции; Санузел, стены А–Г; Санузел, короб инсталляции; по раскладке 157 шт (S = 34,22 м²), с запасом 175 шт
13	Керамогранит матовый R10, тон V486, 600.8×600.8 мм	аналог по характеристикам			м²	15,88		шов 2 мм; Коридор, пол; Прихожая-коридор, пол; по раскладке 39 шт (S = 12,34 м²), с запасом 44 шт
14	Керамогранит матовый, тон F497, 600.8×600.8 мм	аналог по характеристикам			м²	1,80		шов 2 мм; Кухня, фартук (ст. А); по раскладке 4 шт (S = 1,11 м²), с запасом 5 шт
15	Керамогранит матовый R11, тон V486, водопоглощение 0,5 % (BIa), противоскольжение R11, PEI IV	аналог по характеристикам			м²	4,07		13. Балкон 1, пол; количество по площади: S = 3,70 м² + 10 %; клей и затирка — после раскладки плитки
16	Плинтус из керамогранита пола, подрезка 80 мм, верхняя кромка с запилом 45°	аналог по характеристикам			м²	8,46		13. Балкон 1, стены; количество по площади: S = 7,69 м² + 10 %; клей и затирка — после раскладки плитки
	Напольные покрытия							
17	Дуб натуральный брашированный, масло-воск, 14/4 мм, эмиссия E1, укладка на клей	аналог по характеристикам			м²	90		пом. 1, 3, 4, 6, 8, 9, 11, 12; S = 84,06 м² (пол + половина стены в дверных проёмах, как в смете) + 7 %; к заказу — кратно упаковке
18	Клей для паркета и инженерной доски, эластичный (СМП / полиуретановый)	по рекомендации производителя доски			м²	85		площадь приклейки; расход и шпатель — по ТУ клея
	Погонажные изделия							
19	Плинтус МДФ под окраску 80×16 мм, крепление к стене, окраска в цвет Tikkurila F497	аналог по характеристикам			м	99		пом. 1, 3, 4, 6, 8, 9, 11, 12; L = 89,2 м (периметр без дверных проёмов) + 10 % на подрезку; в штуках — по длине планки
20	Плинтус МДФ под окраску 80×16 мм, крепление к стене, окраска в цвет Tikkurila J484	аналог по характеристикам			м	19		пом. 5, 7; L = 16,8 м (периметр без дверных проёмов) + 10 % на подрезку; в штуках — по длине планки
21	Плинтус из керамогранита пола, подрезка 80 мм, верхняя кромка с запилом 45°, h = 80 мм, крепление к стене	аналог по характеристикам			м	9		пом. 13; L = 7,7 м (периметр без дверных проёмов) + 10 % на подрезку; в штуках — по длине планки
	Смеси и материалы для облицовки							
22	Затирка для швов плитки, класс CG2WA по EN 13888	аналог: Mapei Ultracolor 133		аналог:	кг	5,7		по раскладке (a+b)/(a·b) × шов × t × 1,6 + 10 %; в т. ч. 0,1 кг — позиции раскладки без марки
23	Клей плиточный C2 TE S1 по EN 12004, слой 5 мм	аналог: Litokol K80 Eco		аналог:	кг	347		14 меш. по 25 кг; 1,5 кг/м² на 1 мм слоя + 10 %; в т. ч. 8 кг — позиции раскладки без марки
24	Гидроизоляция обмазочная мокрых зон: пол, стены по периметру, зоны замачивания; 2 слоя с армирующей лентой в углах	аналог по характеристикам			м²	16,2		площадь по листу раскладки плитки + 10 %; расход смеси — по ТУ
25	Лента демпферная по периметру пола из плитки	аналог по характеристикам			м	29,1		периметр без дверных проёмов + 10 %

Примечания

1. Количества — из геометрии проекта: площади поверхностей по чистым граням стен до отделки (те же, что в ведомости отделки и колерной карте), плитка, клей и затирка — по раскладке плиточника; в графе «Кол.» — к заказу, с запасом.
2. Краска: расход 0,12 л/м² на слой в 2 слоя, если по ТУ не задан иной; запас 10 % и 0,5 л на подкраску каждого кода. Один код — одна партия, колеровка машинная в колеровочном центре бренда; в заказ — только после утверждения выкраса (колерная карта). Фасовка — по каталогу бренда на дату выпуска; к заказу — не меньше расчётного объёма.
3. «Аналог по характеристикам» — допускается изделие другого производителя с характеристиками не ниже указанных, по согласованию с автором проекта.
4. Графы «Код продукции» и «Масса 1 ед.» не заполнены: коды по классификатору продукции не присвоены, масса единицы до 25 кг (ГОСТ 21.110-2013).
5. Грунтовка и клей для доски указаны площадью обработки; объём — по ТУ выбранного продукта.

	Лист	№ док.	Подпись	Дата	Проект: Четырёхкомнатная квартира			
Дизайнер	Кырлан А.С.			14.11.26	Спецификация отделочных материалов	Стадия	Лист	Листов
Проверил						П	С4	147
Н. контр.								
Утв.								

Список покупок: материалы для магазина

№	Что купить	Артикул или характеристика	Нужно с запасом	Брать в магазине	Фасовка	Уточнить в магазине	Помещения	Кто покупает
Покрытия полов и облицовка								
1	Инженерная доска (дуб натуральный, рабочий слой 4 мм, эмиссия E1, прямая укладка)	по характеристике: дуб натуральный брашированный, масло-воск, 14/4 мм	89,94 м²	90 м²		уточнить в магазине: м² в упаковке	1, 3, 4, 6, 8, 9, 11, 12	по проекту
2	Клей для паркетной и инженерной доски (эластичный, по ТУ изготовителя доски)	на выбор бригады по проекту	84,06 м²			уточнить в магазине: расход и фасовку — по выбранному продукту		бригада
3	Керамогранит 600,8×600,8 мм матовый R10, тон J484	керамогранит матовый R10, тон J484	29 шт	29 шт		уточнить в магазине: штук в коробке	2, 10	по проекту
4	Керамогранит 600,8×600,8 мм матовый, тон F497	по характеристике: керамогранит матовый, тон F497	178 шт	180 шт		уточнить в магазине: штук в коробке	2, 6, 10	по проекту
5	Керамогранит 600,8×600,8 мм матовый R10, тон V486	керамогранит матовый R10, тон V486	43 шт	44 шт		уточнить в магазине: штук в коробке	5, 7	по проекту
6	Керамогранит, R11	по характеристике: керамогранит матовый R11, тон V486, 600×600×10 мм	4,11 м²	4,2 м²		уточнить в магазине: м² в коробке	13	по проекту
Сухие смеси и гидроизоляция								
7	Клей плиточный цементный класса C2 TE S1 (ГОСТ Р 56387-2018)	аналог: Litokol K80 Eco или аналог	346,98 кг	14 меш.	мешок 25 кг			по проекту
8	Затирка цементная класса CG2WA, цвет — по колерной карте	аналог: Mapei Ultracolor 133 или аналог	5,69 кг	3 упак.	упак. 2 кг			по проекту
9	Гидроизоляция обмазочная полимерная, 2 слоя, лента в углах, манжеты на выводах	на выбор бригады по проекту	16,21 м²			уточнить в магазине: расход и фасовку — по выбранному продукту	2, 10	бригада
10	Лента демпферная по периметру пола из плитки	на выбор бригады по проекту	29,06 м	30 м		уточнить в магазине: фасовку		бригада
11	Смесь цементно-песчаная для стяжки М200 (55 мм, 53 мм)	на выбор бригады по проекту	5,55 м³			уточнить в магазине: расход и фасовку — по выбранному продукту		бригада
12	Смесь штукатурная гипсовая для машинного и ручного нанесения по маякам, слой до 10 мм	на выбор бригады по проекту	350,99 м²			уточнить в магазине: расход и фасовку — по выбранному продукту	1, 2, 3, 4, 5, 6, 7, 8, 9, 10, 11, 12, 13	бригада
Короба из ГКЛВ								
13	Лист ГКЛВ 12,5 мм, 2500 × 1200 мм, обшивка коробов в 2 слоя	на выбор бригады по проекту	6,86 м²	3 лист.	лист 3,00 м²		2, 10	бригада
14	Профиль стальной оцинкованный 27 × 28 мм: каркас коробов (стойки и направляющие)	на выбор бригады по проекту	16,69 м	6 шт	хлыст 3 м			бригада
Слаботочные сети								
15	Кабель коаксиальный RG-6 (75 Ом) к розеткам ТВ	на выбор бригады по проекту	14,5 м	15 м		уточнить в магазине: длину бухты		бригада
16	Кабель U/UTP кат. 6 (LAN, Wi-Fi и камеры по PoE)	на выбор бригады по проекту	72,7 м	73 м		уточнить в магазине: длину бухты		бригада
17	Гофротруба Ø20 для слаботочных линий, отдельно от силовых	на выбор бригады по проекту	78,5 м	79 м		уточнить в магазине: длину бухты		бригада
18	Розетка компьютерная RJ45, кат. 6, с рамкой и подрозетником	на выбор бригады по проекту	4 шт	4 шт	шт			бригада
19	Розетка телевизионная (коаксиальная) с рамкой и подрозетником	на выбор бригады по проекту	1 шт	1 шт	шт			бригада
20	Щит слаботочный ЩС: корпус, DIN-рейка, розетки 220 В	на выбор бригады по проекту	1 шт	1 шт	шт			бригада
21	Патч-панель, портов не менее 6	на выбор бригады по проекту	1 шт	1 шт	шт			бригада

	Лист	№ док.	Подпись	Дата	Проект: Четырёхкомнатная квартира			
Дизайнер	Кырлан А.С.			14.11.26				
Проверил					Список покупок	Стадия	Лист	Листов
Н. контр.								
Утв.						П	С5	147

Список покупок: материалы для магазина (продолжение)

№	Что купить	Артикул или характеристика	Нужно с запасом	Брать в магазине	Фасовка	Уточнить в магазине	Помещения	Кто покупает
Лакокрасочные материалы								
22	Краска интерьерная акриловая, матовая, класс истирания 2	Tikkurila Optiva 5 Matt L481 «Silhouette»	9,77 л	4 банк.	банка 2,7 л		1, 11	по проекту
23	Краска интерьерная акриловая, матовая, класс истирания 2	Tikkurila Optiva 5 Matt F497 «Paper»	24,89 л	10 банк.	банка 2,7 л		1, 3, 8, 11, 12	по проекту
24	Краска интерьерная акриловая, глубокоматовая, класс истирания 2	Tikkurila Anti-Reflex 2 F497 «Paper»	21,27 л	8 банк.	банка 2,7 л		1, 3, 4, 5, 7, 8, 9, 11, 12	по проекту
25	Краска интерьерная акриловая, матовая, класс истирания 1	Tikkurila Luja 7 F497 «Paper»	6,8 л	3 банк.	банка 2,7 л		2, 6, 10, 13	по проекту
26	Краска интерьерная акриловая, полуматовая, класс истирания 2	Tikkurila Joker F497 «Paper»	18,27 л	7 банк.	банка 2,7 л		4, 9	по проекту
27	Краска интерьерная акриловая, полуматовая, класс истирания 2	Tikkurila Optiva 20 Semimatt J484 «Castle»	12,14 л	5 банк.	банка 2,7 л		5, 7	по проекту
28	Краска интерьерная акриловая, полуматовая, класс истирания 1	Tikkurila Luja 7 F497 «Paper»	13,46 л	5 банк.	банка 2,7 л		6, 13	по проекту
29	Шпаклёвка финишная полимерная под окраску (стены и потолки, Q3)	на выбор бригады по проекту	430,68 м²			уточнить в магазине: расход и фасовку — по выбранному продукту		бригада
30	Грунтовка акриловая глубокого проникновения, 2 слоя	на выбор бригады по проекту	468 м²			уточнить в магазине: расход и фасовку — по выбранному продукту		бригада
Погонажные изделия и потолки								
31	Плинтус напольный МДФ под покраску, h=80 мм, крепление к стене	по характеристике: плинтус МДФ под окраску 80×16 мм	116,56 м.п.	49 шт	хлыст 2,4 м		1, 3, 4, 5, 6, 7, 8, 9, 11, 12	по проекту
32	Керамогранит на плинтус: полосы h=80 мм из плитки пола, кромка с запилом 45°	по характеристике: плинтус из керамогранита пола, подрезка 80 мм, верхняя кромка с запилом 45°	0,71 м²	0,71 м²		уточнить в магазине: м² в коробке	13	по проекту
33	Потолок подвесной ГКЛ/ГКЛВ по каркасу Knauf П113: листы, профили, подвесы, лента, шпаклёвка швов	Knauf П113	106,37 м²		комплект	уточнить в магазине: расход и фасовку — по выбранному продукту		по проекту
Инженерные изделия								
34	Мат нагревательный электрический для тёплого пола под плитку, с холодным концом и муфтой	на выбор бригады по проекту	1,67 м²			уточнить в магазине: расход и фасовку — по выбранному продукту	2, 10	по проекту
35	Терморегулятор тёплого пола с выносным датчиком пола, монтаж в подрозетник	на выбор бригады по проекту	2 шт	2 шт	шт			по проекту

Примечания

1. «Нужно с запасом» — расход по чертежам и раскладке плюс запас на подрезку и подкраску; «Брать в магазине» — то же количество в единицах, которыми продают (банки, мешки, упаковки, листы, штуки, литры).
2. «Уточнить в магазине» — фасовки этого товара в проекте нет: спросите у продавца, сколько в упаковке, и возьмите целое число упаковок не меньше «Нужно с запасом».
3. Плитку, доску и краску одного цвета берите одной партией (один калибр и тон на помещение) и сохраните чек и номер партии до конца ремонта.
4. «По характеристике» — артикул не выбран: подойдёт любой товар с этими свойствами, согласуйте его с дизайнером до покупки. «Бригада» материал выбирает и закупает бригада по своей технологии.
5. Помещения: 1 — Зал; 2 — Ванная комната; 3 — Тёмная комната; 4 — Детская 1; 5 — Коридор; 6 — Кухня; 7 — Прихожая-коридор; 8 — Гардеробная 2; 9 — Детская 2; 10 — Санузел; 11 — Гостиная; 12 — Гардеробная 1; 13 — Балкон 1; «—» — материал для нескольких помещений, расход по месту.

выпуск 14.11.2026 № e7147312ff · стр. 134 из 147

	Лист	№ док.	Подпись	Дата	Проект: Четырёхкомнатная квартира			
Дизайнер	Кырлан А.С.			14.11.26	Список покупок (окончание)	Стадия	Лист	Листов
Проверил						П	С6	147
Н. контр.								
Утв.								

Смета проекта: весь проект по категориям (цены на 21.09.2026)

Категория	Позиций	С ценой	По КП	Сумма по позициям с ценой, ₽
Ремонт: работы	52	37	15	1 491 794
Ремонт: материалы отделки и черновые	31	16	15	773 036
Электрика: кабель, механизмы, щит	37	0	37	
Сантехника: приборы, трубы, арматура	36	0	36	
Доставка и услуги	4	1	3	77 304
Мебель (включая кухню)	39	0	39	
Свет: светильники и ленты	66	0	66	
Техника	7	0	7	
Декор и текстиль	73	0	73	
ИТОГО по позициям с ценой (цены — нижняя граница открытых прайсов)	**345**	**54**	**291**	**2 342 134**
Резерв на непредвиденные работы и материалы, 15 % от ремонта				351 320
ВЕСЬ ПРОЕКТ — вилка «от … до …», ₽				**2 342 134 … 2 693 454**
Позиции «по КП» — цена не названа, в итог НЕ входят: работы — 15; материалы отделки и черновые — 15; электрика: кабель, механизмы, щит — 37; сантехника: приборы, трубы, арматура — 36; доставка и услуги — 3; мебель (включая кухню) — 39; свет: светильники и ленты — 66; техника — 7; декор и текстиль — 73			**291**	**итог выше на их цену**

По этапам

Этап	Поз.	С ценой	Сумма, ₽
Демонтаж и черновые работы (работы)	10	5	388 965
Инженерные системы (работы)	23	14	207 747
Чистовые работы (работы)	19	18	895 082
Черновые материалы (смеси, ГКЛ, гидроизоляция)	12	2	28 200
Электрика: кабель, механизмы, щит, слаботочка	37	0	
Сантехника: приборы, трубы, арматура	36	0	
Чистовые материалы (отделка, двери)	19	14	744 836
Доставка и услуги	4	1	77 304
Резерв на непредвиденное, 15 %	1	1	351 320
Итого ремонт (с резервом)			**2 693 454**

По помещениям

Помещение	Работы, ₽	Материалы, ₽	Всего, ₽
Общее по объекту (без привязки к помещению)	53 236		53 236
1. Зал	190 465	115 885	306 350
2. Ванная комната	141 635	109 377	251 012
3. Тёмная комната	54 359	21 619	75 978
4. Детская 1	186 203	107 965	294 168
5. Коридор	80 826	24 295	105 121
6. Кухня	174 379	98 106	272 485
7. Прихожая-коридор	105 228	35 372	140 600
8. Гардеробная 2	30 102	10 254	40 356
9. Детская 2	131 467	69 544	201 011
10. Санузел	66 178	47 398	113 576
11. Гостиная	160 723	96 892	257 615
12. Гардеробная 1	52 003	20 417	72 420
13. Балкон 1	64 990	15 912	80 902
Доставка и услуги			77 304
Резерв 15 %			351 320
Итого ремонт (с резервом)			**2 693 454**

	Лист	№ док.	Подпись	Дата	Проект: Четырёхкомнатная квартира			
Дизайнер	Кырлан А.С.			14.11.26	Смета проекта: этапы, помещения, итог	Стадия	Лист	Листов
Проверил						П	С7	147
Н. контр.								
Утв.								

выпуск 14.11.2026 № e7147312ff · стр. 135 из 147

Работы по этапам с расценками (ориентир)

№	Работа	Ед.	Объём	Расценка, ₽	Сумма, ₽	Расценка	Чей подряд
1. Демонтаж и черновые работы — работы, ориентир по открытым прайсам							
1	Демонтаж существующего покрытия пола до основания	м²	106,37	по КП			бригада
2	Демонтаж существующей отделки стен до основания	м²	319,08	по КП			бригада
3	Демонтаж существующей отделки потолка до основания	м²	106,37	по КП			бригада
4	Демонтаж существующих дверных блоков	шт	12,00	по КП			бригада
5	Демонтаж существующих сантехприборов и электрооборудования (если есть)	компл		по КП			бригада
6	Устройство стяжки: стяжка ЦПС М300 (В22,5), фибра, по звукоизоляции, 55 мм	м²	96,70	530	51 251	Ц1	бригада
7	Гидроизоляция обмазочная, 2 слоя: пол, стены на 200 мм, зоны замачивания	м²	14,74	450	6 633	Ц1	бригада
8	Штукатурка стен по маякам, до 10 мм	м²	319,08	530	169 112	Ц1	бригада
9	Штукатурка оконных откосов шириной до 200 мм	м²	4,47	540	2 414	Ц4	бригада
10	Потолок ГКЛ по каркасу П113, 1 слой	м²	106,37	1 500	159 555	Ц1	бригада
2. Инженерные системы — работы, ориентир по открытым прайсам							
11	Прокладка кабеля ВВГнг(А)-LS по группам щита: за потолком и в штробах стен (штробы — только после технического заключения, см. строку «Штробы в стенах»)	м	621,10	60	37 266	Ц3	бригада
12	Прокладка слаботочной линии: Кабель коаксиальный RG-6 (75 Ом) к розеткам ТВ, отдельно от силовых	м	14,50	по КП			бригада
13	Прокладка слаботочной линии: Кабель U/UTP кат. 6 (LAN, Wi-Fi и камеры по PoE), отдельно от силовых	м	72,70	по КП			бригада
14	Прокладка гофротрубы Ø20 для слаботочных линий, отдельно от силовых	м	78,50	140	10 990	Ц3	бригада
15	Сборка слаботочного щита ЩС: корпус, патч-панель, подключение линий и питания 220 В; коммутатор и точки доступа — оборудование заказчика	шт	1,00	по КП			бригада
16	Электроточка: подрозетник в бетоне, розетка, выключатель, вывод	шт	66,00	950	62 700	Ц3	бригада
17	Штробы в стенах под спуски кабеля к точкам — выполняются только после технического заключения о несущих стенах	м	109,90	по КП			бригада
18	Установка встраиваемого точечного светильника	шт	56,00	750	42 000	Ц3	бригада
19	Монтаж светильника: потолочного, подвесного, настенного	шт	7,00	1 200	8 400	Ц3	бригада
20	Монтаж LED-ленты в алюминиевый профиль	м	6,60	230	1 518	Ц3	бригада
21	Установка блока питания LED в доступном месте (люк, шкаф)	шт	2,00	570	1 140	Ц3	бригада
22	Установка автономного пожарного извещателя	шт	7,00	по КП			бригада
23	Сборка щита: установка автоматов и АВДТ групп, вводного автомата	шт	20,00	230	4 600	Ц3	бригада
24	Установка вводного УЗО	шт	1,00	380	380	Ц3	бригада
25	Монтаж инсталляции, установка подвесного унитаза и кнопки смыва	шт	2,00	10 500	21 000	Ц1	бригада
26	Короб инсталляции: каркас и обшивка ГКЛВ в 2 слоя, ревизионный доступ к смыву	шт	2,00	по КП			бригада
27	Короб К1 над чистым полом: каркас и обшивка ГКЛВ под плитку (материалы — в спецификации ВК)	м	5,27	по КП			бригада
28	Установка ванны с сифоном	шт	1,00	6 000	6 000	Ц1	бригада
29	Установка умывальника (мойки) с сифоном и смесителем	шт	3,00	3 000	9 000	Ц1	бригада
30	Подключение стиральной (посудомоечной) машины к ВК	шт	2,00	по КП			бригада
31	Установка радиатора с узлом подключения и терморегулятором	шт	5,00	по КП			бригада
32	Электрический тёплый пол: укладка нагревательного мата в слой клея, датчик пола в гофротрубе	м²	1,67	750	1 253	Ц1	бригада

выпуск 14.11.2026 № e7147312ff · стр. 136 из 147

	Лист	№ док.	Подпись	Дата	Проект: Четырёхкомнатная квартира			
Дизайнер	Кырлан А.С.			14.11.26	Смета проекта: этапы, помещения, итог (продолжение)	Стадия	Лист	Листов
Проверил						П	С8	147
Н. контр.								
Утв.								

Работы по этапам с расценками (ориентир) (продолжение)

№	Работа	Ед.	Объём	Расценка, ₽	Сумма, ₽	Расценка	Чей подряд
33	Установка терморегулятора тёплого пола с датчиком в гофротрубе	шт	2,00	750	1 500	Ц1	бригада
3. Чистовые работы — работы, ориентир по открытым прайсам							
34	Облицовка стен керамогранитом 600,8×600,8 на клею	м²	31,10	2 500	77 750	Ц5	бригада
35	Облицовка короба инсталляции (ГКЛВ) керамогранитом: лицо, боковины, полка	м²	3,12	2 500	7 800	Ц5	бригада
36	Облицовка фартука керамогранитом 600,8×600,8	м²	1,11	2 400	2 664	Ц2	бригада
37	Укладка керамогранита на пол, 600×600, на клею	м²	23,33	1 800	41 994	Ц2	бригада
38	Затирка швов керамогранита	м²	58,25	150	8 738	Ц2	бригада
39	Грунтование стен, 2 слоя (под штукатурку и под отделку)	м²	319,08	96	30 632	Ц4	бригада
40	Шпаклёвка стен под окраску, 2 слоя (старт и финиш), уровень К3	м²	285,16	750	213 870	Ц1	бригада
41	Грунтование и шпаклёвка оконных откосов, 2 слоя	м	28,21	300	8 463	Ц4	бригада
42	Грунтование потолка, 2 слоя	м²	106,37	96	10 212	Ц4	бригада
43	Шпаклёвка потолка под окраску, 2 слоя, уровень Q3	м²	106,37	950	101 052	Ц1	бригада
44	Окраска потолка водно-дисперсионной краской, 2 слоя	м²	106,37	360	38 293	Ц1	бригада
45	Окраска стен водно-дисперсионной краской, 2 слоя	м²	332,41	300	99 723	Ц1	бригада
46	Окраска оконных откосов, 2 слоя	м	28,21	120	3 385	Ц4	бригада
47	Укладка инженерной доски на клей	м²	84,07	1 200	100 884	Ц1	бригада
48	Установка плинтуса МДФ h=80 мм	м	105,96	450	47 682	Ц1	бригада
49	Плинтус из керамогранита: нарезка полос из плитки пола, запил кромки 45°, установка h=80 мм	м	7,69	930	7 152	Ц2	бригада
50	Окраска плинтуса в тоне F497, 2 слоя	м	105,96	300	31 788	Ц1	бригада
51	Монтаж межкомнатных дверей (поставщик дверей)	шт	12,00	5 250	63 000	Ц1	поставщик
52	Монтаж телевизора ОБ-01 на кронштейн, скрытая прокладка HDMI и питания (штроба, трубка), подключение акустики	шт	1,00	по КП			бригада
4. Прочие работы и услуги — работы, ориентир по открытым прайсам							
53	Кухонный гарнитур по проекту кухни, изготовление и монтаж (4–8 нед.)	компл	1,00	по КП			поставщик
	Итого работы (позиции с расценкой)				**1 491 794**		

Примечания

1. Итог «ВЕСЬ ПРОЕКТ» — не прогноз, а сумма того, у чего есть цена: ремонт (работы и материалы по смете сметчика), мебель, свет, техника и декор — по ценам из данных проекта. Позиции без цены названы «по КП» (291 шт.) и в итог не входят: пока цена не названа, итог выше напечатанного.
2. Вилка: «от» — сумма по позициям с ценой по нижней границе открытых прайсов (цены на 21.09.2026, Москва); «до» — «от» плюс резерв на непредвиденное (15 % от ремонта; частный ремонт 10–20 %).
3. Работы — ориентир по прайсам подрядчиков, не договорная цена: расценку называет бригада после контрольного обмера. Материалы — по «Смете материалов с ценами» (следующий лист).
4. Разбивка по помещениям — доли: общая закупка делится пропорционально площади (длине, числу), по которой считается позиция; работы — по объёму строки в помещении. Сумма по помещениям, по этапам и по категориям одна и та же.
5. Источники расценок и цен: Ц1 — Домашний мастерок: прайс на отделочные работы, 2026; Ц2 — Домашний мастерок: прайс на плиточные работы, 2026; Ц3 — Домашний мастерок: прайс на электромонтажные работы, 2026; Ц4 — Профи ремонтник: штукатурно-малярные работы; Ц5 — Profi.ru: укладка керамогранита на стены, Москва 2026; Ц6 — справочник материалов: ориентир по сегментам; Ц7 — Розница Москвы, 09.2026: Лемана ПРО, KGSnab, официальный дилер Farrow & Ball.
6. Оборудование «по КП» из сметы сметчика (кухня и др.): 1 поз. — в позиции «по КП» мебели и техники.

	Лист	№ док.	Подпись	Дата	Проект: Четырёхкомнатная квартира			
Дизайнер	Кырлан А.С.			14.11.26				
Проверил					Смета проекта: этапы, помещения, итог (окончание)	Стадия	Лист	Листов
Н. контр.								
Утв.						П	С9	147

выпуск 14.11.2026 № e7147312ff · стр. 137 из 147

Смета материалов с ценами

№	Позиция	Ед.	Нетто	Запас	С запасом	К закупке (упаковка)	Цена за ед., ₽	Сумма, ₽	Заказать заранее	Доп.
Чистовая отделка — позиций 19, с ценой 14, итого 744 836 ₽										
Покрытия полов и облицовка										
1	Инженерная доска (дуб натуральный, рабочий слой 4 мм, эмиссия E1, прямая укладка) — дуб натуральный брашированный, масло-воск, 14/4 мм	м²	84,06	7 %	89,94	90,00 м²	4 513 / м²	406 170		1, 7
2	Керамогранит 600,8×600,8 мм матовый R10, тон J484 — керамогранит матовый R10, тон J484	шт	26	12 %	29	29 шт · коробка	1 800 / м²	18 846		7
3	Керамогранит 600,8×600,8 мм матовый, тон F497 — керамогранит матовый, тон F497	шт	161	12 %	180	180 шт · коробка	1 800 / м²	116 946		1, 7
4	Керамогранит 600,8×600,8 мм матовый R10, тон V486 — керамогранит матовый R10, тон V486	шт	39	13 %	44	44 шт · коробка	1 800 / м²	28 584		7
5	Керамогранит, R11 — керамогранит матовый R11, тон V486, 600×600×10 мм	м²	3,74	10 %	4,11	4,20 м²	1 800 / м²	7 560		1, 7
Лакокрасочные материалы										
6	Краска интерьерная акриловая, матовая, класс истирания 2 — Tikkurila Optiva 5 Matt L481 «Silhouette»	л	8,88	10 %	9,77	4 банка · банка 2,7 л	3 510 / банк	14 040		7
7	Краска интерьерная акриловая, матовая, класс истирания 2 — Tikkurila Optiva 5 Matt F497 «Paper»	л	22,63	10 %	24,89	10 банка · банка 2,7 л	3 510 / банк	35 100		7
8	Краска интерьерная акриловая, глубокоматовая, класс истирания 2 — Tikkurila Anti-Reflex 2 F497 «Paper»	л	19,34	10 %	21,27	8 банка · банка 2,7 л	3 510 / банк	28 080		7
9	Краска интерьерная акриловая, матовая, класс истирания 1 — Tikkurila Luja 7 F497 «Paper»	л	6,18	10 %	6,80	3 банка · банка 2,7 л	3 510 / банк	10 530		7
10	Краска интерьерная акриловая, полуматовая, класс истирания 2 — Tikkurila Joker F497 «Paper»	л	16,61	10 %	18,27	7 банка · банка 2,7 л	3 510 / банк	24 570		7
11	Краска интерьерная акриловая, полуматовая, класс истирания 2 — Tikkurila Optiva 20 Semimatt J484 «Castle»	л	11,04	10 %	12,14	5 банка · банка 2,7 л	3 510 / банк	17 550		7
12	Краска интерьерная акриловая, полуматовая, класс истирания 1 — Tikkurila Luja 7 F497 «Paper»	л	12,24	10 %	13,46	5 банка · банка 2,7 л	3 510 / банк	17 550		7
Погонажные изделия и потолки										
13	Плинтус напольный МДФ под покраску, h=80 мм, крепление к стене — плинтус МДФ под окраску 80×16 мм	м	105,96	10 %	116,56	49 шт · хлыст 2,4 м	368 / шт	18 032		1, 7
14	Керамогранит на плинтус: полосы h=80 мм из плитки пола, кромка с запилом 45° — плинтус из керамогранита пола, подрезка 80 мм, верхняя кромка с запилом 45°	м²	0,62	15 %	0,71	0,71 м²	1 800 / м²	1 278		1, 7
Двери										
15	Дверь межкомнатная Д-1, проём 900×2100 мм	шт	6		6	6 шт	по запросу			6
16	Дверь межкомнатная Д-2, проём 700×2100 мм	шт	3		3	3 шт	по запросу			6
17	Дверь межкомнатная Д-3, проём 600×2100 мм	шт	1		1	1 шт	по запросу			6
18	Дверь раздвижная Д-4, проём 1420×2100 мм	шт	1		1	1 шт	по запросу			6
19	Дверь межкомнатная Д-5, проём 730×2100 мм	шт	1		1	1 шт	по запросу			6
Черновые материалы — позиций 12, с ценой 2, итого 28 200 ₽										
Покрытия полов и облицовка										
20	Клей для паркетной и инженерной доски (эластичный, по ТУ изготовителя доски)	м²	84,06		84,06	фасовка по ТУ изделия	по запросу			2
Сухие смеси и гидроизоляция										
21	Клей плиточный цементный класса C2 TE S1 (ГОСТ Р 56387-2018) — аналог: Litokol K80 Eco или аналог	кг	315,44	10 %	346,98	14 мешок · мешок 25 кг	1 800 / меш.	25 200		7
22	Затирка цементная класса CG2WA, цвет — по колерной карте — аналог: Mapei Ultracolor 133 или аналог	кг	5,17	10 %	5,69	3 упаковка · упак. 2 кг	1 000 / упак.	3 000		7
23	Гидроизоляция обмазочная полимерная, 2 слоя, лента в углах, манжеты на выводах	м²	14,74	10 %	16,21	фасовка по ТУ изделия	по запросу			2
24	Лента демпферная по периметру пола из плитки	м	26,42	10 %	29,06	30,00 м	по запросу			
25	Смесь цементно-песчаная для стяжки М200 (55 мм, 53 мм)	м³	5,29	5 %	5,55	фасовка по ТУ изделия	по запросу			2
26	Смесь штукатурная гипсовая для машинного и ручного нанесения по маякам, слой до 10 мм	м²	319,08	10 %	350,99	фасовка по ТУ изделия	по запросу			2

	Лист	№ док.	Подпись	Дата	Проект: Четырёхкомнатная квартира			
Дизайнер	Кырлан А.С.			14.11.26				
Проверил					Смета материалов с ценами	Стадия	Лист	Листов
Н. контр.								
Утв.						П	С10	147

Смета материалов с ценами (продолжение)

№	Позиция	Ед.	Нетто	Запас	С запасом	К закупке (упаковка)	Цена за ед., ₽	Сумма, ₽	Заказать заранее	Доп.
Короба из ГКЛВ										
27	Лист ГКЛВ 12,5 мм, 2500 × 1200 мм, обшивка коробов в 2 слоя	м²	6,24	10 %	6,86	3 лист · лист 3,00 м²	по запросу			
28	Профиль стальной оцинкованный 27 × 28 мм: каркас коробов (стойки и направляющие)	м	15,17	10 %	16,69	6 шт · хлыст 3 м	по запросу			
Лакокрасочные материалы										
29	Шпаклёвка финишная полимерная под окраску (стены и потолки, Q3)	м²	391,53	10 %	430,68	фасовка по ТУ изделия	по запросу			2
30	Грунтовка акриловая глубокого проникновения, 2 слоя	м²	425,45	10 %	468,00	фасовка по ТУ изделия	по запросу			2
Погонажные изделия и потолки										
31	Потолок подвесной ГКЛ/ГКЛВ по каркасу Knauf П113: листы, профили, подвесы, лента, шпаклёвка швов	м²	106,37		106,37	фасовка по ТУ изделия	по запросу			2
Электрика и слаботочные сети — позиций 37, с ценой 0, итого 0 ₽										
Слаботочные сети										
32	Кабель коаксиальный RG-6 (75 Ом) к розеткам ТВ	м	14,50		14,50	15,00 м	по запросу			3
33	Кабель U/UTP кат. 6 (LAN, Wi-Fi и камеры по PoE)	м	72,70		72,70	73,00 м	по запросу			3
34	Гофротруба Ø20 для слаботочных линий, отдельно от силовых	м	78,50		78,50	79,00 м	по запросу			3
35	Розетка компьютерная RJ45, кат. 6, с рамкой и подрозетником	шт	4		4	4 шт	по запросу			
36	Розетка телевизионная (коаксиальная) с рамкой и подрозетником	шт	1		1	1 шт	по запросу			
37	Щит слаботочный ЩС: корпус, DIN-рейка, розетки 220 В	шт	1		1	1 шт	по запросу			
38	Патч-панель, портов не менее 6	шт	1		1	1 шт	по запросу			
Инженерные изделия										
39	Мат нагревательный электрический для тёплого пола под плитку, с холодным концом и муфтой	м²	1,67		1,67	фасовка по ТУ изделия	по запросу			2
40	Терморегулятор тёплого пола с выносным датчиком пола, монтаж в подрозетник	шт	2		2	2 шт	по запросу			
Электрика: силовая часть										
41	Кабель силовой ВВГнг(А)-LS 3×1,5 мм²	м	307,40		307,40	308,00 м	по запросу			3
42	Кабель силовой ВВГнг(А)-LS 3×2,5 мм²	м	303,90		303,90	304,00 м	по запросу			3
43	Кабель силовой ВВГнг(А)-LS 3×6 мм²	м	9,80		9,80	10,00 м	по запросу			3
Электрика: щит										
44	Автоматический выключатель дифференциального тока (АВДТ) C10 A, 30 мА, тип A	шт	5		5	5 шт	по запросу			4
45	Автоматический выключатель дифференциального тока (АВДТ) C16 A, 30 мА, тип A	шт	13		13	13 шт	по запросу			4
46	Автоматический выключатель дифференциального тока (АВДТ) C32 A, 30 мА, тип A	шт	1		1	1 шт	по запросу			4
47	Корпус щита ЩРВ-П-72, IP41, навесной, 72 модулей	шт	1		1	1 шт	по запросу			4
48	Вводной автомат C63, 1P+N	шт	1		1	1 шт	по запросу			4
49	Вводное УЗО-А 63 А, 100 мА (селективное)	шт	1		1	1 шт	по запросу			4
50	УЗИП тип 2	шт	1		1	1 шт	по запросу			4
Электрика: механизмы и изделия										
51	Розетка с з/к и защитными шторками, 16 А	шт	46		46	46 шт	по запросу			4
52	Розетка IP44 с крышкой, 16 А	шт	3		3	3 шт	по запросу			4

	Лист	№ док.	Подпись	Дата
Дизайнер	Кырлан А.С.			14.11.26
Проверил				
Н. контр.				
Утв.				

Проект: Четырёхкомнатная квартира

Смета материалов с ценами (продолжение)

Стадия	Лист	Листов
П	С11	147

Смета материалов с ценами (продолжение)

№	Позиция	Ед.	Нетто	Запас	С запасом	К закупке (упаковка)	Цена за ед., ₽	Сумма, ₽	Заказать заранее	Доп.
53	Выключатель 1-клав.	шт	4		4	4 шт	по запросу			4
54	Выключатель 1-клав. проходной	шт	3		3	3 шт	по запросу			4
55	Выключатель 2-клав.	шт	5		5	5 шт	по запросу			4
56	Выключатель 2-клав. (проходная + обычная)	шт	1		1	1 шт	по запросу			4
57	Выключатель 2-клав. проходной	шт	2		2	2 шт	по запросу			4
58	Светорегулятор 1-канальный, задний фронт (LED)	шт	1		1	1 шт	по запросу			4
59	Рамка 1-постовая	шт	43		43	43 шт	по запросу			4
60	Рамка 2-постовая	шт	11		11	11 шт	по запросу			4
61	Терморегулятор тёплого пола	шт	2		2	2 шт	по запросу			4
62	Коробка установочная (подрозетник) Ø68	шт	67		67	67 шт	по запросу			4
63	Вывод кабеля под прибор (клеммник)	шт	5		5	5 шт	по запросу			4
64	Коробка уравнивания потенциалов КУП	шт	2		2	2 шт	по запросу			4
65	Блок питания LED 24 В, 100 Вт, дим.	шт	1		1	1 шт	по запросу			4
66	Блок питания LED 24 В, 30 Вт	шт	1		1	1 шт	по запросу			4
67	Извещатель дымовой автономный	шт	4		4	4 шт	по запросу			4
68	Извещатель тепловой	шт	3		3	3 шт	по запросу			4
Сантехника — позиций 36, с ценой 0, итого 0 ₽										
Сантехника: санитарные приборы										
69	Ванна встраиваемая акриловая 1700×750 мм, с каркасом, экраном и отверстием слив-перелив — акриловая 1700×750, смеситель настенный термостатический	шт	1		1	1 шт	по запросу			5
70	Унитаз подвесной безободковый, с сиденьем микролифт, крепёж и звукоизолирующая прокладка	шт	2		2	2 шт	по запросу			5, 1
71	Инсталляция для подвесного унитаза: рама высотой 1120 мм, бачок, клавиша смыва (ось клавиши 1050 мм от чистого пола)	шт	2		2	2 шт	по запросу			5, 1
72	Умывальник подвесной 550×450 мм, с отверстием под смеситель и переливом	шт	1		1	1 шт	по запросу			5, 1
73	Умывальник подвесной 400×200 мм, с отверстием под смеситель и переливом	шт	1		1	1 шт	по запросу			5, 1
74	Мойка кухонная врезная 760×480 мм, с переливом	шт	1		1	1 шт	по запросу			5, 1
75	Полотенцесушитель электрический, IP44, с терморегулятором	шт	1		1	1 шт	по запросу			5, 1
Сантехника: смесители, сифоны и арматура приборов										
76	Смеситель для ванны настенный однорычажный, межосевое 150 мм, с душевым набором (лейка, шланг, держатель)	шт	1		1	1 шт	по запросу			5, 1
77	Смеситель для умывальника однорычажный, с донным клапаном	шт	2		2	2 шт	по запросу			5, 1
78	Смеситель кухонный однорычажный, высокий излив	шт	1		1	1 шт	по запросу			5, 1
79	Обвязка ванны слив-перелив Ø40/50 с сифоном	шт	1		1	1 шт	по запросу			5, 1
80	Сифон для умывальника бутылочный Ø32/40–50, с гофрой к выпуску	шт	2		2	2 шт	по запросу			5, 1
81	Сифон для мойки Ø40/50	шт	1		1	1 шт	по запросу			5, 1
82	Сифон для посудомоечной машины с обратным клапаном, на выводе слива Ø40	шт	1		1	1 шт	по запросу			5, 1
83	Сифон для стиральной машины встраиваемый в стену Ø50, с обратным клапаном	шт	1		1	1 шт	по запросу			5, 1

	Лист	№ док.	Подпись	Дата	Проект: Четырёхкомнатная квартира			
Дизайнер	Кырлан А.С.			14.11.26	Смета материалов с ценами (продолжение)	Стадия	Лист	Листов
Проверил						П	С12	147
Н. контр.								
Утв.								

Смета материалов с ценами (продолжение)

№	Позиция	Ед.	Нетто	Запас	С запасом	К закупке (упаковка)	Цена за ед., ₽	Сумма, ₽	Заказать заранее	Доп.
84	Кран угловой ½"×½" с гибкой подводкой 40 см (умывальники, мойка)	шт	6		6	6 шт	по запросу			5, 1
85	Кран шаровой угловой ½"×¾" для подключения стиральной и посудомоечной машины	шт	2		2	2 шт	по запросу			5, 1
Сантехника: трубопроводы										
86	Труба полипропиленовая PP-R PN20 Ø20×3,4 (B1) — ГОСТ 32415-2013	м	24,50	10 %	24,50	24,50 м	по запросу			5
87	Труба PP-R, армированная стекловолокном, PN20 Ø20×2,8 (T3) — ГОСТ 32415-2013	м	19,50	10 %	19,50	19,50 м	по запросу			5
88	Труба канализационная ПП Ø40 (К1) — ГОСТ 32414-2013	м	5,00	10 %	5,00	5,00 м	по запросу			5
89	Труба канализационная ПП Ø50 (К1) — ГОСТ 32414-2013	м	12,50	10 %	12,50	12,50 м	по запросу			5
90	Труба канализационная ПП Ø110 (К1) — ГОСТ 32414-2013	м	5,00	10 %	5,00	5,00 м	по запросу			5
Сантехника: фасонные части и выводы										
91	Отвод канализационный ПП 45° Ø40 — ГОСТ 32414-2013	шт	4		4	4 шт	по запросу			5
92	Отвод канализационный ПП 45° Ø50 — ГОСТ 32414-2013	шт	10		10	10 шт	по запросу			5
93	Отвод канализационный ПП 45° Ø110 — ГОСТ 32414-2013	шт	10		10	10 шт	по запросу			5
94	Тройник канализационный ПП 45° (врезки ветвей) — ГОСТ 32414-2013	шт	7		7	7 шт	по запросу			5
95	Ревизия канализационная ПП (после поворота трассы) — ГОСТ 32414-2013	шт	6		6	6 шт	по запросу			5
96	Фитинги PP-R Ø20: тройники, угольники 90° (ветви и повороты B1, T3) — ГОСТ 32415-2013	шт	28		28	28 шт	по запросу			5
97	Водорозетка PP-R Ø20×½" настенная, с креплением — ГОСТ 32415-2013	шт	12		12	12 шт	по запросу			5
Сантехника: узлы ввода, люки, короба										
98	Кран шаровой латунный Ду15 PN16 (отключение ввода)	шт	4		4	4 шт	по запросу			5, 1
99	Фильтр сетчатый косой Ду15	шт	4		4	4 шт	по запросу			5, 1
100	Счётчик воды крыльчатый Ду15 (ХВ, ГВ), с поверкой	шт	4		4	4 шт	по запросу			5, 1
101	Клапан обратный Ду15	шт	4		4	4 шт	по запросу			5, 1
102	Люк ревизионный нажимной под плитку 300×400 мм	шт	4		4	4 шт	по запросу			5, 1
103	Звукоизоляция стояка К1 в коробе: рулонный звукоизоляционный материал ≥ 10 мм, обмотка стояка на высоту этажа	м	5,40		5,40	5,40 м	по запросу			5, 1
104	Короб К1 над полом: профиль ПН/ПС, ГКЛВ 12,5 мм под плитку	м	5,80		5,80	5,80 м	по запросу			5, 1
	ИТОГО материалы (позиций с ценой 16 из 104; без цены 88 — «по запросу», в итог не входят)							**773 036**		


Примечания

1. Количества — из единой книги материалов проекта: тот же расход, что в спецификации отделочных материалов, смете и списке покупок. Запас — на подрезку и бой; норма запаса печатается в графе «Запас», её основание — в отдельном документе «Смета на материалы».
2. Цены — нижняя граница открытых прайсов (цены на 21.09.2026, Москва); не предложение (оферта) магазинов. Цены нет — «по запросу», позиция в итог не входит. Работы в эту смету не входят (они — на листе «Смета проекта»).
3. Доп. 1. Изделие не выбрано: позиция описана по характеристикам («аналог»); марка, артикул и цена определяются при выборе изделия.
4. Доп. 2. Фасовка не задана в данных: количество дано в мерах расчёта, число упаковок определяется по выбранному продукту (расход и тара — по ТУ).
5. Доп. 3. Длина кабеля — по длинам групп щита из данных электрика; запас на подрезку в длину не заложен — берите бухту с запасом 5–10 %.
6. Доп. 4. Механизмы, рамки и подрозетники — по ведомости изделий электрика; серию механизмов выбирает заказчик.
7. Доп. 5. Трубы и фасонные части — по трассам листа разводки, +10 % на подрезку (уже в количестве); модели приборов заказчик выбирает сам.
8. Доп. 6. Двери: цена и срок называет поставщик после выбора изделия; в смету стоят только если цена задана в данных.
9. Доп. 7. Цена — нижняя граница открытых прайс-листов на дату сбора (книга цен проекта); не коммерческое предложение магазина.
10. Доп. 8. Доли по помещениям справочные: общая закупка делится пропорционально площади (длине, числу), по которой считается позиция.

	Лист	№ док.	Подпись	Дата	Проект: Четырёхкомнатная квартира			
Дизайнер	Кырлан А.С.			14.11.26	Смета материалов с ценами (окончание)	Стадия	Лист	Листов
Проверил						П	С13	147
Н. контр.								
Утв.								

1 Порог 15 мм: мокрая зона — смежное помещение (М 1:5)


Применение: двери

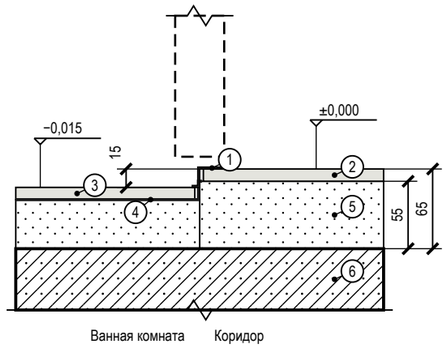

Поз.	Состав слоя, изделие
1	порог-переход металлический, перепад 15 мм, на клей-герметик
2	керамогранит 600×600×10
3	керамогранит 600×600×10
4	гидроизоляция в 2 слоя с подъёмом на торец ступени, лента в углу
5	ЦПС М300 (В22,5) 55 мм; в мокрой зоне 40 мм
6	плита перекрытия

2 Стык покрытий пола Т-профилем без перепада (М 1:10)


Применение: проёмы 3↔5, 4↔5, 6↔7, 7↔8, 8↔7, 9↔7

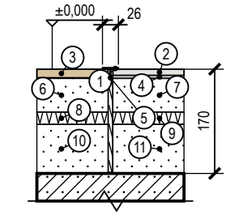

Поз.	Состав слоя, изделие
1	Т-профиль алюминиевый, полка 26 мм, ножка в шов; цвет — по покрытию
2	Коридор: керамогранит 600×600×10
3	Тёмная комната: инженерная доска дуб на клею
4	Коридор: клей плиточный С2 TE S1 5 мм
5	шов 8 мм по оси полотна двери, заполнитель эластичный
6	Тёмная комната: стяжка ЦПС М300 (В22,5), фибра, по звукоизоляции 55 мм
7	Коридор: стяжка ЦПС М300 (В22,5), фибра, по звукоизоляции 55 мм
8	Тёмная комната: звукоизоляция — минплита 110 кг/м³ 20 мм
9	Коридор: звукоизоляция — минплита 110 кг/м³ 20 мм
10	Тёмная комната: засыпка керамзитовая фр. 0–5, уплотнённая 80 мм
11	Коридор: засыпка керамзитовая фр. 0–5, уплотнённая 80 мм

3 Короб стояков К1-1, В1-1, Т3-1 с люком и звукоизоляцией (М 1:20)


Применение: пом. 9

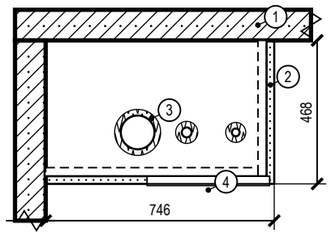

Поз.	Состав слоя, изделие
1	стены существующие — не ослаблять
2	короб: профиль 27×28, ГКЛВ 2×12,5 мм, облицовка плиткой
3	звукоизоляция стояков рулонная 20 мм; К1-1 Ø110, В1-1 Ø32, Т3-1 Ø25
4	ревизионный люк 400×600 мм нажимной, под плитку; против ревизии стояка

4 Гидроизоляция санузла: заход на стены 200 мм, примыкание ванны (М 1:20)


Применение: пом. 2, 10

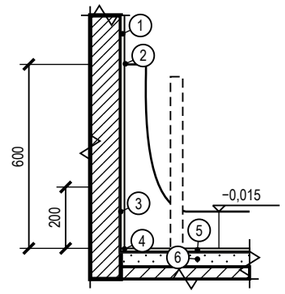

Поз.	Состав слоя, изделие
1	облицовка — плитка на клею С2 TE S1, затирка CG2WA
2	примыкание ванны: лента бордюрная + силиконовый санитарный герметик; облицовка опирается на борт
3	гидроизоляция обмазочная в 2 слоя, заход на стены 200 мм (в зоне душа — выше), до облицовки; акт скрытых работ, тест проливом
4	лента гидроизоляционная в углах и у трапов
5	керамогранит 600×600×10
6	стяжка ЦПС 50 мм

5 Плинтус МДФ 80×16 мм у окрашенной стены по доске (ламинату) (М 1:10)


Применение: пом. 1, 3, 4, 6, 8, 9, 11, 12

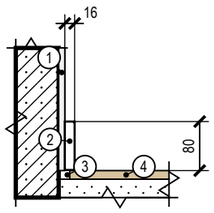

Поз.	Состав слоя, изделие
1	штукатурка, шпаклёвка Q3, окраска — по ведомости отделки
2	плинтус МДФ 80×16 под окраску в цвет стены; клей монтажный — к стене, не к полу
3	зазор покрытия у стены 8–10 мм закрывается плинтусом
4	инженерная доска дуб на клею

6 Плинтус МДФ 80×16 мм у окрашенной стены по керамограниту (плитке) (М 1:10)

Применение: пом. 5, 7

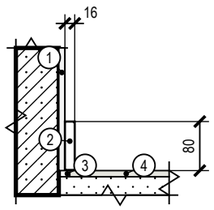

Поз.	Состав слоя, изделие
1	штукатурка, шпаклёвка Q3, окраска — по ведомости отделки
2	плинтус МДФ 80×16 под окраску в цвет стены; клей монтажный — к стене, не к полу
3	зазор покрытия у стены 8–10 мм закрывается плинтусом
4	керамогранит 600×600×10

Условные обозначения

- железобетон (плита, стены) — условно: конструкция не установлена
- кладка, перегородка — условно: конструкция не установлена
- стяжка, раствор
- гипсокартон ГКЛВ
- звукоизоляция, эластичный заполнитель
- плитка, керамогранит на клею
- инженерная доска (покрытие пола)
- металлический профиль (порог, Т-профиль, короб двери)
- гидроизоляция (обмазочная, лента)

Примечания

1. Узлы — типовые решения проекта для мест, отмеченных выносками на листе схемы расположения развёрток и узлов; размеры — в мм, отметки — в м от ±0,000.
2. Узлы с гидроизоляцией, закладными и коробами скрытого монтажа принимаются по актам скрытых работ до закрытия отделкой; гидроизоляция — после теста проливом (24 ч).
3. Марки изделий (порог, Т-профиль, короб скрытой двери, люк) — по спецификациям; замена — на аналог с теми же габаритами по согласованию с автором проекта.
4. Материал плиты перекрытия и стен в узлах показан условно (железобетон, кладка): конструкция дома не установлена — крепёж, анкеры и толщины слоёв уточняются после обследования (до него — по допущениям общих указаний).

	Лист	№ док.	Подпись	Дата
Дизайнер	Кырлан А.С.			14.11.26
Проверил				
Н. контр.				
Утв.				


Проект: Четырёхкомнатная квартира

Узлы

Стадия	Лист	Листов
П	С14	147

выпуск 14.11.2026 № e7147312ff · стр. 142 из 147

№	Работа	Нед.	После
Р-1	**демонтаж**	1,5	
Р-2	**контрольный обмер**	0,5	Р-1
Р-3	**черновая электрика**	2,25	Р-2
Р-4	черновая сантехника	1,5	Р-2
Р-5	**штукатурка**	3	Р-3, Р-4
Р-6	**стяжка**	1,25	Р-5
Р-7	**гидроизоляция**	0,75	Р-6
Р-8	ГКЛ	2,25	Р-3, Р-4
Р-9	**плитка**	4,25	Р-7, Р-8, Р-6
Р-10	**шпаклёвка**	3,5	Р-9, Р-8, Р-5
Р-11	**окраска**	2,75	Р-10
Р-12	**чистовые полы**	1,5	Р-11, Р-9
Р-13	**двери и плинтусы**	1,25	Р-12, Р-11
Р-14	**чистовая электрика и сантехника**	1,25	Р-13, Р-11
Р-15	**кухня и мебель**	1,5	Р-14, Р-13
Р-16	**сдача**	1	Р-15, Р-14
Закупки: заказать не позднее — «◆»; от заказа до поставки — штриховая полоса; срок поставки — только из данных или «ориентир практики»			
З-1	Кухонный гарнитур по проекту кухни: модули М-19, М-20, М-21, М-22, М-23, М-24, М-25, М-27	6	для Р-15
З-2	Встраиваемая техника кухни: М-19 холодильник, М-21 духовой шкаф, М-24 вытяжка, М-26 посудомоечная		для Р-15
З-3	Стиральная машина: ОБ-02 (вертикальная загрузка 400 × 600 мм — условие закупки)		для Р-4
З-4	Сантехнические приборы и инсталляции: С-01, С-02, С-03, С-05, С-06, С-07		для Р-4
З-5	Керамогранит и плитка: 3 поз. по артикулу и формату, 54,55 м² по раскладке		для Р-9
З-6	Покрытие пола (доска) и плинтус: пом. 1, 3, 4, 6, 8, 9, 11, 12		для Р-12
З-7	Встроенная мебель по замеру цеха: М-08, М-09, М-15, М-18, М-30, М-33, М-34, М-36, М-40, М	6	для Р-15

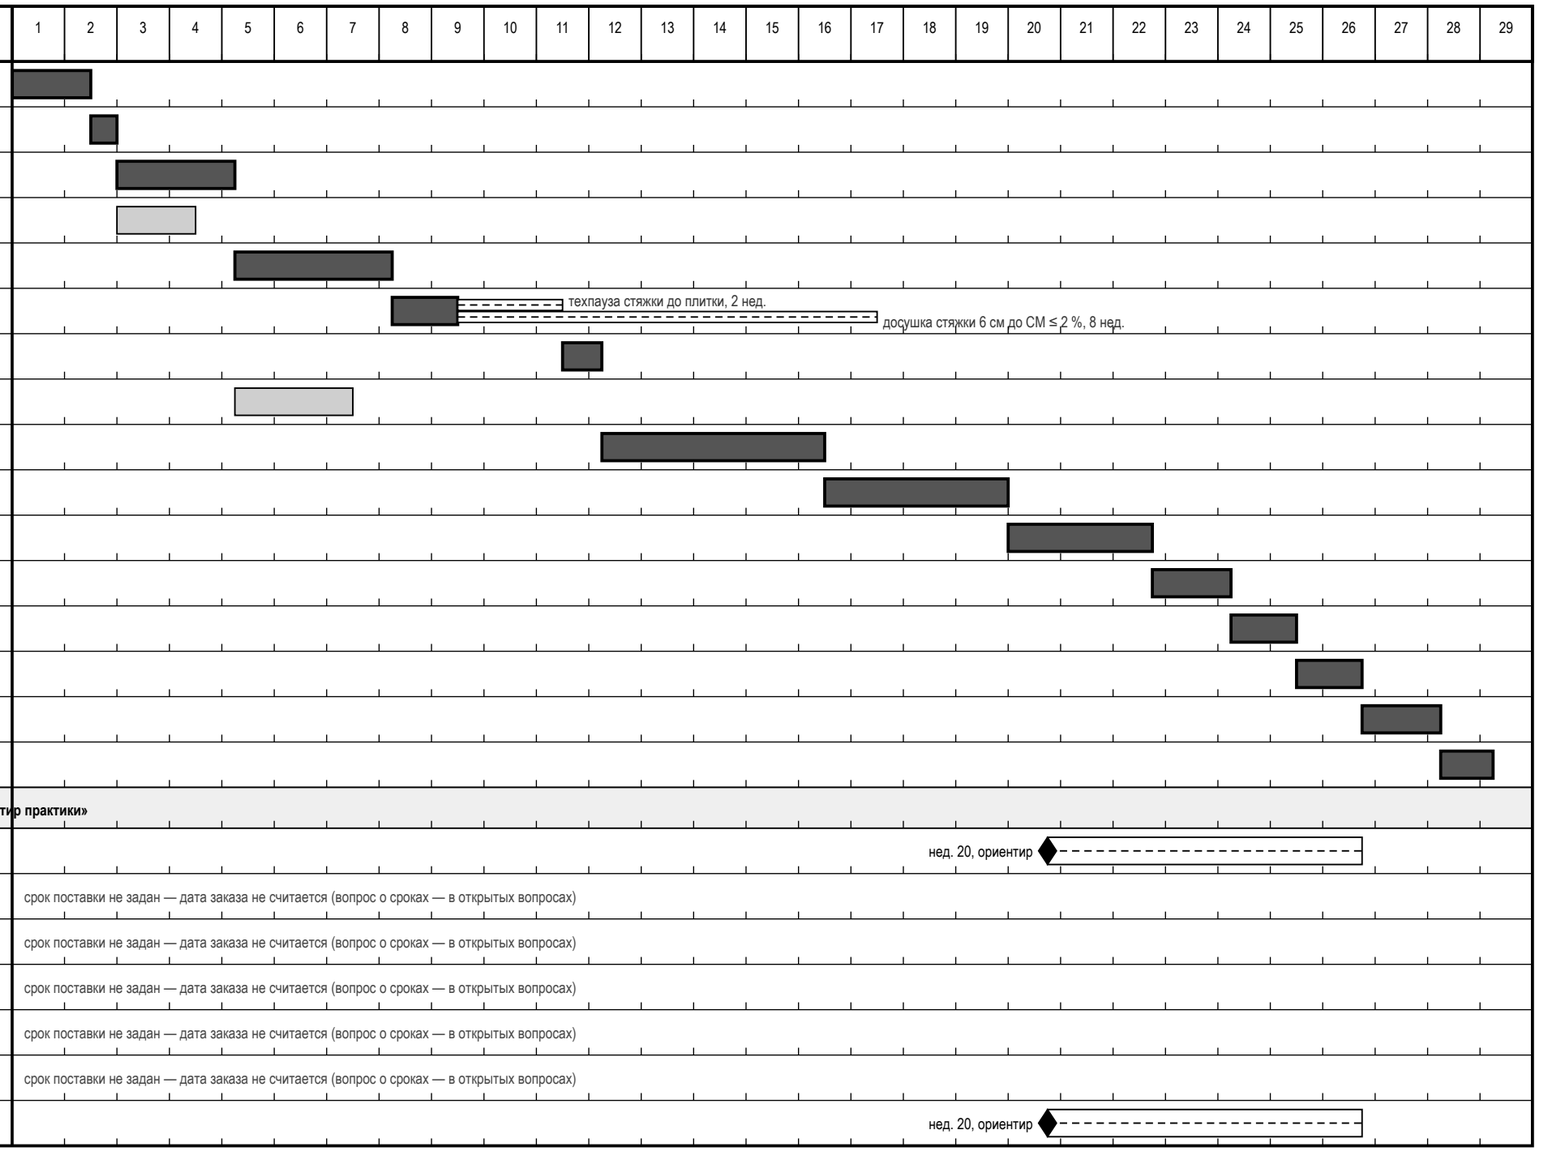

Итого: ≈ 28,25 нед. · жирная линия и тёмная полоса — критический путь

Примечания

1. Длительности этапов — типовые сроки по площади 102,67 м² (таблица «Свод для графика»: недели по этапам для 45, 80 и 120 м², середина вилки, линейная интерполяция); это ориентир, а не норма и не обещание бригады. Контрольный обмер — ориентир 0,5 нед. (в таблице нет).
2. Зависимости «после» — из графика закупок и работ (лист «График закупок и работ»); каждая работа начинается после конца предшественников. Техпаузы стоят отдельными полосами, а не спрятаны в длительности: стяжка → плитка — не менее 2 нед.; стяжка → чистовой пол — досушка стяжки 6 см до СМ ≤ 2 % — 8 нед. (ориентир «1 нед. на 1 см до 4 см, 5 см — 6 нед., 6 см — 8 нед.»; решает замер).
3. График последовательный и поэтому консервативный: в жизни шпаклёвка, плитка и досушка стяжки идут частично параллельно (таблица типовых сроков для 102,67 м²: 19–25 нед.). Совмещения — решение прораба после обмера.
4. Закупки: «заказать не позднее» = начало работы, которой нужна позиция, минус срок поставки. Срок поставки — из данных проекта (срок поставки позиции, срок изготовления обоев в отделке); если его нет, в графике стоит типовой диапазон практики с пометкой «ориентир» — это не срок поставщика, его надо получить до заказа. Кухню и встроенную мебель заказывают после замера по готовым стенам (после штукатурки). Позиции без срока дат заказа не имеют.

	Лист	№ док.	Подпись	Дата	Проект: Четырёхкомнатная квартира			
Дизайнер	Кырлан А.С.			14.11.26	Календарный график работ и закупок	Стадия	Лист	Листов
Проверил						П	С15	147
Н. контр.								
Утв.								

выпуск 14.11.2026 № e7147312ff · стр. 143 из 147

Приёмка по этапам: контрольные точки, допуски и акты скрытых работ

Этап	Контрольная точка (дальше не пускают без подписи)	Что проверяют	Чем	Допуск	Основание	Подпись	Акт скрытых работ / документ
Р-1	Демонтаж До начала демонтажа: запрошены документы на дом и БТИ	Что снимается и что не трогается: покрытия, отделка, дверные блоки; несущие стены и перегородки — без изменений	осмотр по плану демонтажа	снятое — только по плану; несущее не затрагивать	практика		Фото помещений до и после демонтажа; перечень снятого в журнале работ.
Р-2	Контрольный обмер Контрольный обмер на голых стенах сделан до заказа всего, что делают по размеру	Размеры помещений и проёмов, диагонали, положение стояков, щитка, каналов, толщины стен	рулетка, лазерный дальномер, уровень	допуск задаёт проект; расхождение с планом — в перечень открытых вопросов до заказа	практика		Протокол контрольного обмера с эскизом; расхождения занесены в открытые вопросы.
Р-3	Черновая электрика Черновая электрика: трассы, высоты подрозетников, замер изоляции подписаны до заделки	Сопротивление изоляции проводки (цепи до 1000 В)	мегаомметр	не менее 0,5 МОм	норматив (ПУЭ, гл. 1.8)		Акт скрытых работ на трассы проводки и слаботочные линии до закрытия штукатуркой и ГКЛ; исполнительная схема трасс с привязками; заземление и уравнивание потенциалов в санузле протокол и фото.
		Целостность и маркировка: PE жёлто-зелёный, N — синий, L — прочие цвета	визуально, прозвонка	каждый проводник промаркирован	практика		
		Высоты подрозетников и привязки — по плану розеток и выключателей	рулетка, уровень	по проекту; от чистого пола	практика		
Р-4	Черновая сантехника Черновая сантехника: опрессовка, отметки выводов, инсталляции подписаны до зашивки	Опрессовка водоснабжения: рабочее давление до 0,6 МПа — испытание 0,9 МПа; выше 0,6 МПа — по расчёту	опрессовочный насос, манометр	выдержка 10 мин (поквартирная); падение: пластик не более 0,06 МПа за 30 мин, сталь не более 0,05 МПа за 10 мин	практика (СП 73.13330)		Акт опрессовки (давление, время, результат); акт скрытых работ на трассы в стенах, полу и коробах; инсталляции, скрытые смесители, трапы — фото с рулеткой и отметками.
		Уклон канализации Ø40–50	уровень, построитель плоскостей	не менее 20 мм на 1 м	норматив (СП 30.13330)		
		Протечки в соединениях, сифоны, смесители, гибкая подводка	осмотр под давлением, салфетка на стыках	нет капель и влажных следов в контрольное время	практика		
		Отметки выводов и положение инсталляций до зашивки и гидроизоляции	рулетка в кадре, фото	по листу выводов	практика		
Р-5	Штукатурка Маяки стен проверены до штукатурки; коробки скрытых дверей стоят до штукатурки	Отклонение от вертикали (простая / улучшенная / высококачественная штукатурка)	отвес, лазерный уровень	3 / 2 / 1 мм на 1 м; не более 15 / 10 / 5 мм на высоту	практика (СП 71.13330.2017)		Фото коробок скрытых дверей с отметкой чистого пола — до штукатурки; класс штукатурки (простая / улучшенная / высококачественная) назван в договоре.
		Отклонение от горизонтали	уровень, правило	3 / 2 / 1 мм на 1 м; не более 15 / 10 / 5 мм на длину	практика (СП 71.13330.2017)		
		Неровности (плоскостность)	правило 2 м и щуп	до 5 / 3 / 2 мм на 1 м; не более 3 / 2 / 2 неровностей на 4 м²	практика (СП 71.13330.2017)		
		Влажность основания перед шпаклёвкой и отделкой	влагомер	верхние 20–30 мм — не более 5 % по массе	норматив (СП 71, табл. 7.2)		
Р-6	Стяжка Стяжка: подготовка, после заливки ровность, затем замер СМ перед чистовым полом	Ровность: просвет под рейкой 2 м	рейка 2 м, клиновой щуп	под паркет, ламинат — 2 мм; под гидроизоляцию до 4 мм; прочие покрытия — до 6 мм (цифры расходятся между источниками — сверить перед актом)	практика (СП 29.13330)		Акт скрытых работ на стяжку (толщина, армирование) до чистового пола; протокол ровности и протокол СМ-влажности; звукоизоляция и демпферная лента под стяжкой — фото и паспорт; контуры тёплого пола до заливки — схема укладки и замер сопротивления.
		Отклонение от горизонтали по помещению	уровень, нивелир	не более 0,2 % длины помещения	практика (СП 29.13330)		

	Лист	№ док.	Подпись	Дата	Проект: Четырёхкомнатная квартира			
Дизайнер	Кырлан А.С.			14.11.26	Чек-лист приёмки по этапам. Лист 1 из 3	Стадия	Лист	Листов
Проверил						П	С16	147
Н. контр.								
Утв.								

выпуск 14.11.2026 № e7147312ff · стр. 144 из 147

Приёмка по этапам: контрольные точки, допуски и акты скрытых работ (продолжение)

Этап	Контрольная точка (дальше не пускают без подписи)	Что проверяют	Чем	Допуск	Основание	Подпись	Акт скрытых работ / документ
		Число точек измерения	рейка	не менее 3 на 30 м² или 1 на небольшое помещение	практика		
		Отслоения и пустоты	простукивание молотком или киянкой	глухой звук — зона вскрывается и переделывается	практика		
		Влажность перед укладкой доски: цементная стяжка	влагомер; СМ-замер	ЦПС не более 2,0 % СМ (с тёплым полом не более 1,8 %); влагомер для плитки — не более 5 %	практика (СП 71; рекомендации производителей)		
Р-7	Гидроизоляция Гидроизоляция: пролив 24 ч подпись до плитки	Заведение на стены не ниже 200 мм от чистого пола; за ванной — 300 мм выше борта; в душе без поддона — на высоту лейки	рулетка	не менее 200 мм	норматив (СП 71.13330.2017, п. 8.6.5); остальное — практика		Акт теста проливом, фото узлов и высоты заведения на стены — до плитки.
		Тест проливом: слой воды 10–30 мм, контроль уровня и потолка соседа снизу	линейка, визуально	24 ч (минимум 12 ч); падения уровня и протечки нет	практика		
		Два слоя обмазки с межслойной сушкой, лента в углах и манжеты на выводах	визуально	по инструкции производителя	практика		
Р-8	ГКЛ Короба, ниши и потолки: черновые сети в зоне коробов приняты до обшивки	Шаг саморезов, отступ от кромки, заделка стыков (как у перегородок)	рулетка, визуально	потолок 150 мм; кромка 5–10 мм; стык — лента и 2 слоя шпаклёвки	практика (СП 163.1325800.2014)		Акт скрытых работ: каркас ГКЛ, закладные, звукоизоляция — фото до обшивки; воздуховоды в коробах и за потолком — фото и схема.
		Закладные под тяжёлое, карнизы, подвесные светильники на месте до обшивки	фото с привязками	по плану потолков и узлам	практика		
		Ревизионные люки: доступ к арматуре и ревизиям сохранён	осмотр	по листу ВК	практика		
Р-9	Плитка Раскладка плитки: первая плита и первый ряд проверены по развёртке; плитка выбрана, калибр партии измерен	Уступы между смежными плитками	линейка, на просвет	не более 1 мм	норматив (СП 71.13330.2017)		Раскладка подписана до начала плитки; протокол первого ряда; акт теста проливом приложен (этап гидроизоляции).
		Ширина шва и его прямолинейность	линейка, калибр	до 6 мм ручная укладка; фактическая по проекту ±0,5 мм	практика		
		Отклонение рядов от вертикали и горизонтали	уровень, правило, отвес	1,5 мм на 1 м длины	практика		
		Ровность облицовки	правило 2 м и щуп	не более 2–4 мм (цифра расходится по источникам)	практика		
		Пустоты под плиткой	простукивание всей площади	до 10 % площади допустимо; свыше 25 % под одной плиткой — брак	практика		
Р-10	Шпаклёвка Шпаклёвка Q3/Q4: проверка боковым светом до окраски	Класс основания под окраску: Q3 — сплошное финишное шпаклевание; Q4 — под направленный свет	переносной прожектор у поверхности под острым углом	Q3: царапины от абразива до 0,5 мм; Q4 — без видимых царапин и теней; неровность на 2 м: Q3 — 1 мм, Q4 — 0,5 мм	практика (Q-классы — не норматив СП, а согласованный критерий)		Класс (Q3 или Q4) назван в договоре; грунтование и армирование стыков перед шпаклёвкой — запись в журнале.
Р-11	Окраска Выкрасы утверждены, колеровка одной партией	Окраска без полос, подтёков, пропусков; цвет — по колерной карте	боковой свет, образец выкраса	без видимых дефектов при боковом свете	практика		Утверждённые выкрасы; остаток колеровки одной партии — для подкраски.
		Основание сухое, огрунтованное; защита от прямого солнца при высыхании	осмотр	по ТУ краски	норматив (СП 71.13330.2017, п. 7.5.2)		

	Лист	№ док.	Подпись	Дата	Проект: Четырёхкомнатная квартира			
Дизайнер	Кырлан А.С.			14.11.26	Чек-лист приёмки по этапам. Лист 2 из 3	Стадия	Лист	Листов
Проверил						П	С17	147
Н. контр.								
Утв.								

выпуск 14.11.2026 № e7147312ff · стр. 145 из 147

Приёмка по этапам: контрольные точки, допуски и акты скрытых работ (продолжение)

Этап	Контрольная точка (дальше не пускают без подписи)	Что проверяют	Чем	Допуск	Основание	Подпись	Акт скрытых работ / документ
P-12	Чистовые полы Чистовые полы: влажность, ровность, уступы, зазоры — до укладки доски; мокрые работы закончены	Деформационный зазор у стен и порогов (доска, ламинат)	линейка, клинья при укладке	8–15 мм (чаще 10 мм); у ламината 5–10 мм по СП 71	практика (требования производителей); норматив (СП 71, п. 8.10.14)		Протокол СМ-влажности стяжки до укладки; паспорт и партия доски.
		Перепад основания под покрытие	правило 2 м и щуп	не более 2 мм на 2 м	практика		
		Зазоры и перепады между досками; скрип; видимый зазор в замке — брак	щуп, рука, шаг	«ступеньки» нет	практика		
		Влажность помещения при укладке и после	гигрометр	не более 60 %, без сквозняков	норматив (СП 71, п. 8.1.7)		
P-13	Двери и плинтусы Полотна и плинтусы — после чистового пола; скрытые полотна после чистовой отделки стен	Отклонение коробки от вертикали	отвес, уровень	1,5 мм на 1 м, не более 3 мм на коробку	практика (ТР 105-00, пересказ)		Коробки скрытых дверей приняты до штукатурки (этап штукатурки); паспорт на полотна.
		Зазор между полотном и коробкой по периметру	щуп	2–4 мм по бокам и верху (единого норматива нет)	практика		
		Открывание и закрывание: без перекоса, плавный ход петель и доводчика	визуально, от руки	без задевания коробки и пола	практика		
P-14	Чистовая электрика и сантехника Чистовая электрика и сантехника: протокол электролаборатории и проверка УЗО до подписи акта	УЗО: кнопка «Тест»; время отключения; ток отключения	кнопка на аппарате; прибор проверки УЗО (не мультиметр)	отключает; не более 0,3 с; 50–100 % от IΔn	практика измерений		Протокол измерений аккредитованной электролаборатории (изоляция по группам, УЗО, PE, фаза-ноль); исполнительная схема щита; акт опрессовки приложен (этап ВК).
		Сопротивление изоляции готовых линий; петля фаза-ноль для срабатывания автоматов	мегаомметр; прибор петли фаза-ноль	изоляция не менее 0,5 МОм; петля — по проекту	норматив (ПУЭ, гл. 1.8) / по проекту		
		Смесители, сифоны, гибкая подводка: пробный пуск воды	визуально под нагрузкой	нет подтёков в контрольное время	практика		
P-15	Кухня и мебель Кухня и мебель: замер кухни снят по готовым стенам; чистовая электрика и сантехника подведены	Привязка выводов и розеток к модулям кухни; вытяжка, вентиляция	рулетка, сверка с листом кухни	по проекту кухни	практика		Акт передачи кухни; паспорта техники и гарантийные талоны.
		Тяга вентиляции у решёток	лист бумаги у решётки	бумага притягивается; при сомнениях — замер анемометром	практика		
P-16	Сдача Финальная приёмка по таблицам СП 71: дефектная ведомость и акт	Стены, потолки, полы, плитка, двери, окна осмотр по чек-листу этапов выше	правило 2 м, уровень, щуп, боковой свет, влагомер	по таблицам выше	практика		Дефектная ведомость и акт приёмки; гарантия: по умолчанию претензии по качеству работ — 2 года, в договоре прописывается отдельно.
		Полный пакет документов: акты скрытых работ, протокол электролаборатории, акт опрессовки, исполнительные схемы, гарантийные обязательства	комплектность	пакет собран до подписи акта	практика		

Примечания

1. Метка основания: «норматив» — цифра подтверждена текстом СП, ГОСТ или ПУЭ; «практика» — отраслевая конвенция или один источник: к спору не годится без сверки первоисточника (СП 71.13330.2017, СП 29.13330, СП 163.1325800.2014, ПУЭ гл. 1.8, СП 73.13330, СП 30.13330).
2. Класс штукатурки (простая / улучшенная / высококачественная) и класс основания под окраску (Q3 или Q4) называются в договоре подряда: допуск выбирается по ним. Q-классы — не норматив, а согласованный сторонами критерий.
3. Акт скрытых работ подписывают до того, как работа закрыта следующим слоем (штукатуркой, плиткой, стяжкой, обшивкой): постфактум он слабее — осматривать нечего. Подписывают заказчик (или технадзор), подрядчик; при перепланировке — автор проекта. Каждую зону снимают до закрытия с рулеткой в кадре и привязкой к стене.
4. По умолчанию, если срок не прописан в договоре, претензии по качеству работ можно предъявить в течение 2 лет со дня приёмки; в договоре гарантийный срок и сроки на скрытые работы рекомендуется назвать явно.

	Лист	№ док.	Подпись	Дата	Проект: Четырёхкомнатная квартира			
Дизайнер	Кырлан А.С.			14.11.26	Чек-лист приёмки по этапам. Лист 3 из 3	Стадия	Лист	Листов
Проверил						П	С18	147
Н. контр.								
Утв.								

выпуск 14.11.2026 № e7147312ff · стр. 146 из 147

Какому мастеру какие листы (номера — как в штампе)

Мастер	Что делает по альбому	Листы	Кроме чертежей — документы	Листов
Замерщик и прораб (до начала работ)	Контрольный обмер на голых стенах, сверка размеров и диагоналей, ответы на открытые вопросы до заказа	19–20, 22, 107–112	Задание на контрольный обмер; лист открытых вопросов	9
Гипсокартонщик и монтажник перегородок	Демонтаж и возведение перегородок, каркас, короба инсталляции, ниши, потолки; закладные под навесное	23–28, 51–55	Ведомость материалов каркаса; акт скрытых работ на каркас	11
Электрик	Группы щита, подрозетники и высоты, трассы, свет, управление светом, слаботочка, тёплый пол	56–64, 70–106	Таблица нагрузок; ведомость изделий; протокол электролаборатории	46
Сантехник	Выводы воды и канализации, разводка, аксонометрии, инсталляции, короба стояков	39–46, 70–106	Спецификация ВК; акт опрессовки; акт пролива	45
Монтажник вентиляции, отопления и кондиционеров	Вентиляция, радиаторы и тёплые полы, кондиционеры: места, размеры, трассы и дренаж	65–66	Акт опрессовки азотом (кондиционеры); фото воздуховодов до закрытия	2
Штукатур, шпаклёвщик, маляр, паркетчик	Основание стен, окраска и обои по колерной карте, полы и пороги, плинтус, узлы стыков	29–31, 67, 70–106, С1–С4, С14	Колерная карта и выкрасы; спецификация отделочных материалов	46
Плиточник	Раскладка и подрезка плитки стен, пола и фартука, гидроизоляция, швы, выводы в плитке	44–45, 47–48, 68–106, С14	Ведомость плитки; акт теста проливом	44
Монтажник дверей и окон	Заполнение проёмов: размеры коробок, открывание, пороги, скрытые двери	49–50	Ведомость проёмов; паспорта на полотна	2
Мебельщик, кухонный монтажник	Кухня и мебель на заказ: габариты, членение, фурнитура, связка с электрикой и сантехникой	24–28, 32–38, Д1–Д16	Ведомость изделий; замер кухни по готовым стенам	28
Заказчик и комплектатор	Что и когда покупать, сколько с запасом, во что это обойдётся; свет, декор и текстиль; визуализации как должно получиться	1–18, 21, 63, С5–С13, С15	Список покупок; смета; календарный график	30
Прораб и технадзор (приёмка)	Приёмка этапов, акты скрытых работ, дефектная ведомость	С15–С19	Чек-лист приёмки по этапам; календарный график	5

Примечания

1. Номера листов — как в основной надписи: основные подряд (1, 2, 3…), «Д» — детализация мебели, «С» — ведомости, спецификации, узлы и сметы, «П» — приложение единого комплекта. «12–18» — все листы с 12 по 18.
2. Лист может быть у нескольких мастеров: развёртка стены нужна электрику (высоты точек), сантехнику (выводы), отделочнику (материалы) и плиточнику (раскладка). Общие листы (обмер, список листов, перечень вопросов) прораб раздаёт всем.
3. Мастер работает по чертежам и берёт в руки то, что назначено ему здесь; закупки, смету и график ведёт заказчик с прорабом. Лист, которого нет в таблице ни у одного мастера, — вопрос прорабу: чей он.

	Лист	№ док.	Подпись	Дата	Проект: Четырёхкомнатная квартира			
Дизайнер	Кырлан А.С.			14.11.26	Лист → мастер	Стадия	Лист	Листов
Проверил						П	С19	147
Н. контр.								
Утв.								

выпуск 14.11.2026 № e7147312ff · стр. 147 из 147