
L

LINEA

ДИЗАЙН-ПРОЕКТ ИНТЕРЬЕРА

Квартира 101 м²

ретро с авторской мебелью

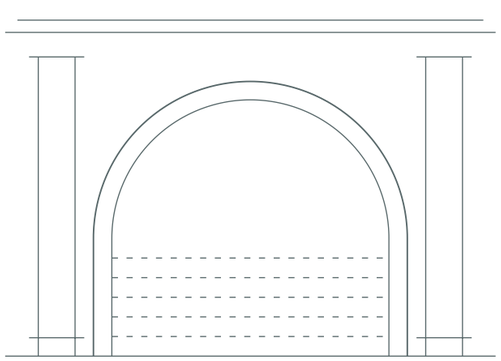

ПАЛИТРА ОТДЕЛКИ

F&B No. 291	NCS S 0502-Y	F&B No. 289	F&B No. 255	NCS S 1005-Y20
58 %	29 %	10 %	3 %	текстиль, декор

АВТОР ПРОЕКТА

Кырлан Александр Сергеевич

Ноябрь 2026



Визуализация гостиной · 3D

ОБЩАЯ ПЛОЩАДЬ	ПОМЕЩЕНИЙ	СТАДИЯ	ШИФР	ОСНОВА
100,72 м²	11, из них жилых 4	Проект · предварительно	ГД-2026-009-АИ	план заказчика, без обмера

Как оставить правку: кнопка «Правка к этому листу» в правом верхнем углу любого листа · все листы проекта: дизайн-студия-квартир.рф/review.html?p=gost-retro103

выпуск 14.11.2026 № 32d0256903 · стр. 1 из 129

Объект

Квартира 103 м²: 100,72 м², помещений 11, из них жилых 4.

Стиль: мид-сенчури 65 %, ар-деко 35 %. Стадия: предварительный альбом без обмера, планировка по плану заказчика.

Открытых вопросов 7, конфликтов разделов 0; изменений утверждено 2, ждут подписи 0.

Розетки и выводы

38 розеток (рамок 33), 6 выводов кабеля под технику и свет, 14 групп щита — всё с высотами от чистого пола: листы 56, 59.

Что решено (подписано вами)

ИЗ-1 — Группы 7 (санузлы: фены, полотенцесушители, УЗО 10 мА) и 8 (стиральная машина постирочной) добавлены, точки переназначены.

ИЗ-2 — Д-9 открывается из ванной в спальню (петли у начала проёма).

Что ждёт вашего ответа

вопросов 7; блокируют заказ или работы — 3, они первыми и выделены

№	Вопрос	Варианты · что будет без ответа	Нужен ответ
К-1	Размеры сняты со скана обмерного плана KV оформление (в см): часть подписей не читается, помещения выровнены по читаемым размерам.	Без ответа: размеры на листах — по плану заказчика, уточняются по месту; мебель на заказ и материалы по ним не заказывать.	**до заказа мебели и дверей**
К-6	Ванная мастер (пом. 11): стояки Ст К1-3 Ø110, Ст В1-3, Ст Т3-3 по данным стоят в углу стен В и Г (оси ≈ 90–240 мм от стены Г, 150–280 мм от стены В) — внутри габарита душевого…	Затем решить: (а) короб стояков в углу ≈ 310 × 350 с люком, поддон 800 × 800 сдвинуть вдоль стены В от короба, стеклоблочную перегородку разобрать и выложить заново по новому поддону; (б) поддон меньше, вне короба (по…	**до начала этих работ**
К-7	Унитаз подвесной С-02 (пом. 6 «Ванная»), выпуск К1-2 Ø110: трасса до Ст К1-1 (1,91 м) идёт под дверным проёмом Д-5 — короб над полом там не поставить.	Решить: (а) прибор ближе к стояку Ст К1-1 (без прохода под проёмом); (б) выпуск в полу с подъёмом пола помещения на 160 мм; (в) насосная установка (КНС) у прибора — по паспорту, требует согласования. Без ответа: выпуск К1-2…	**до начала этих работ**
К-2	Высота потолка принята 2650 мм по отметкам обмера (Н = 2,50…2,66 м).	Без ответа: высоты на развёртках и потолки — от 2650 мм, уточнить при обмере.	до выпуска рабочей документации
К-4	Разрешённая мощность объединённой квартиры по ТУ неизвестна, принята 15 кВт.	Без ответа: щит и группы рассчитаны на 15 кВт; при меньших ТУ — пересчёт.	до выпуска рабочей документации
К-5	Объединение двух квартир в одну (проём в межквартирной стене между гостиной и коридором правой квартиры, вход — один из тамбура, второй вход закрывается.	Без ответа: проём и перегородки — предложение, к строительству не выдаются; мокрые зоны и кухня оставлены на местах обмера.	до демонтажа и возведения перегородок
К-8	Климатический подрайон (СП 131.13330) не задан: принят не северный — жилые комнаты и кухня под потолком от 2,5 м (СП 54, п. 5.12).	Без ответа: отметки потолков жилых — по 2,5 м; при северном подрайоне уровни ниже 2,7 м пересчитать до заказа каркаса.	до заказа каркаса потолков

Полный текст каждого вопроса, варианты и рекомендация — на листах 103, 104 реестра открытых вопросов.

	Лист	№ док.	Подпись	Дата	Проект: Квартира 103 м²			
Дизайнер	Кырлан А.С.			14.11.26	Ваш проект на одной странице	Стадия	Лист	Листов
Проверил						П	2	129
Н. контр.								
Утв.								



	Лист	№ док.	Подпись	Дата	Проект: Квартира 103 м²			
Дизайнер	Кырлан А.С.			14.11.26				
Проверил					Визуализация: Кабинет-библиотека	Стадия	Лист	Листов
Н. контр.								
Утв.						П	3	129

выпуск 14.11.2026 № 32d0256903 · стр. 3 из 129




	Лист	№ док.	Подпись	Дата	Проект: Квартира 103 м²			
Дизайнер	Кырлан А.С.			14.11.26				
Проверил					Визуализация: Кабинет-библиотека	Стадия	Лист	Листов
Н. контр.								
Утв.						П	4	129

выпуск 14.11.2026 № 32d0256903 · стр. 4 из 129



	Лист	№ док.	Подпись	Дата	Проект: Квартира 103 м²			
Дизайнер	Кырлан А.С.			14.11.26				
Проверил					Визуализация: Кабинет-библиотека	Стадия	Лист	Листов
Н. контр.								
Утв.						П	5	129

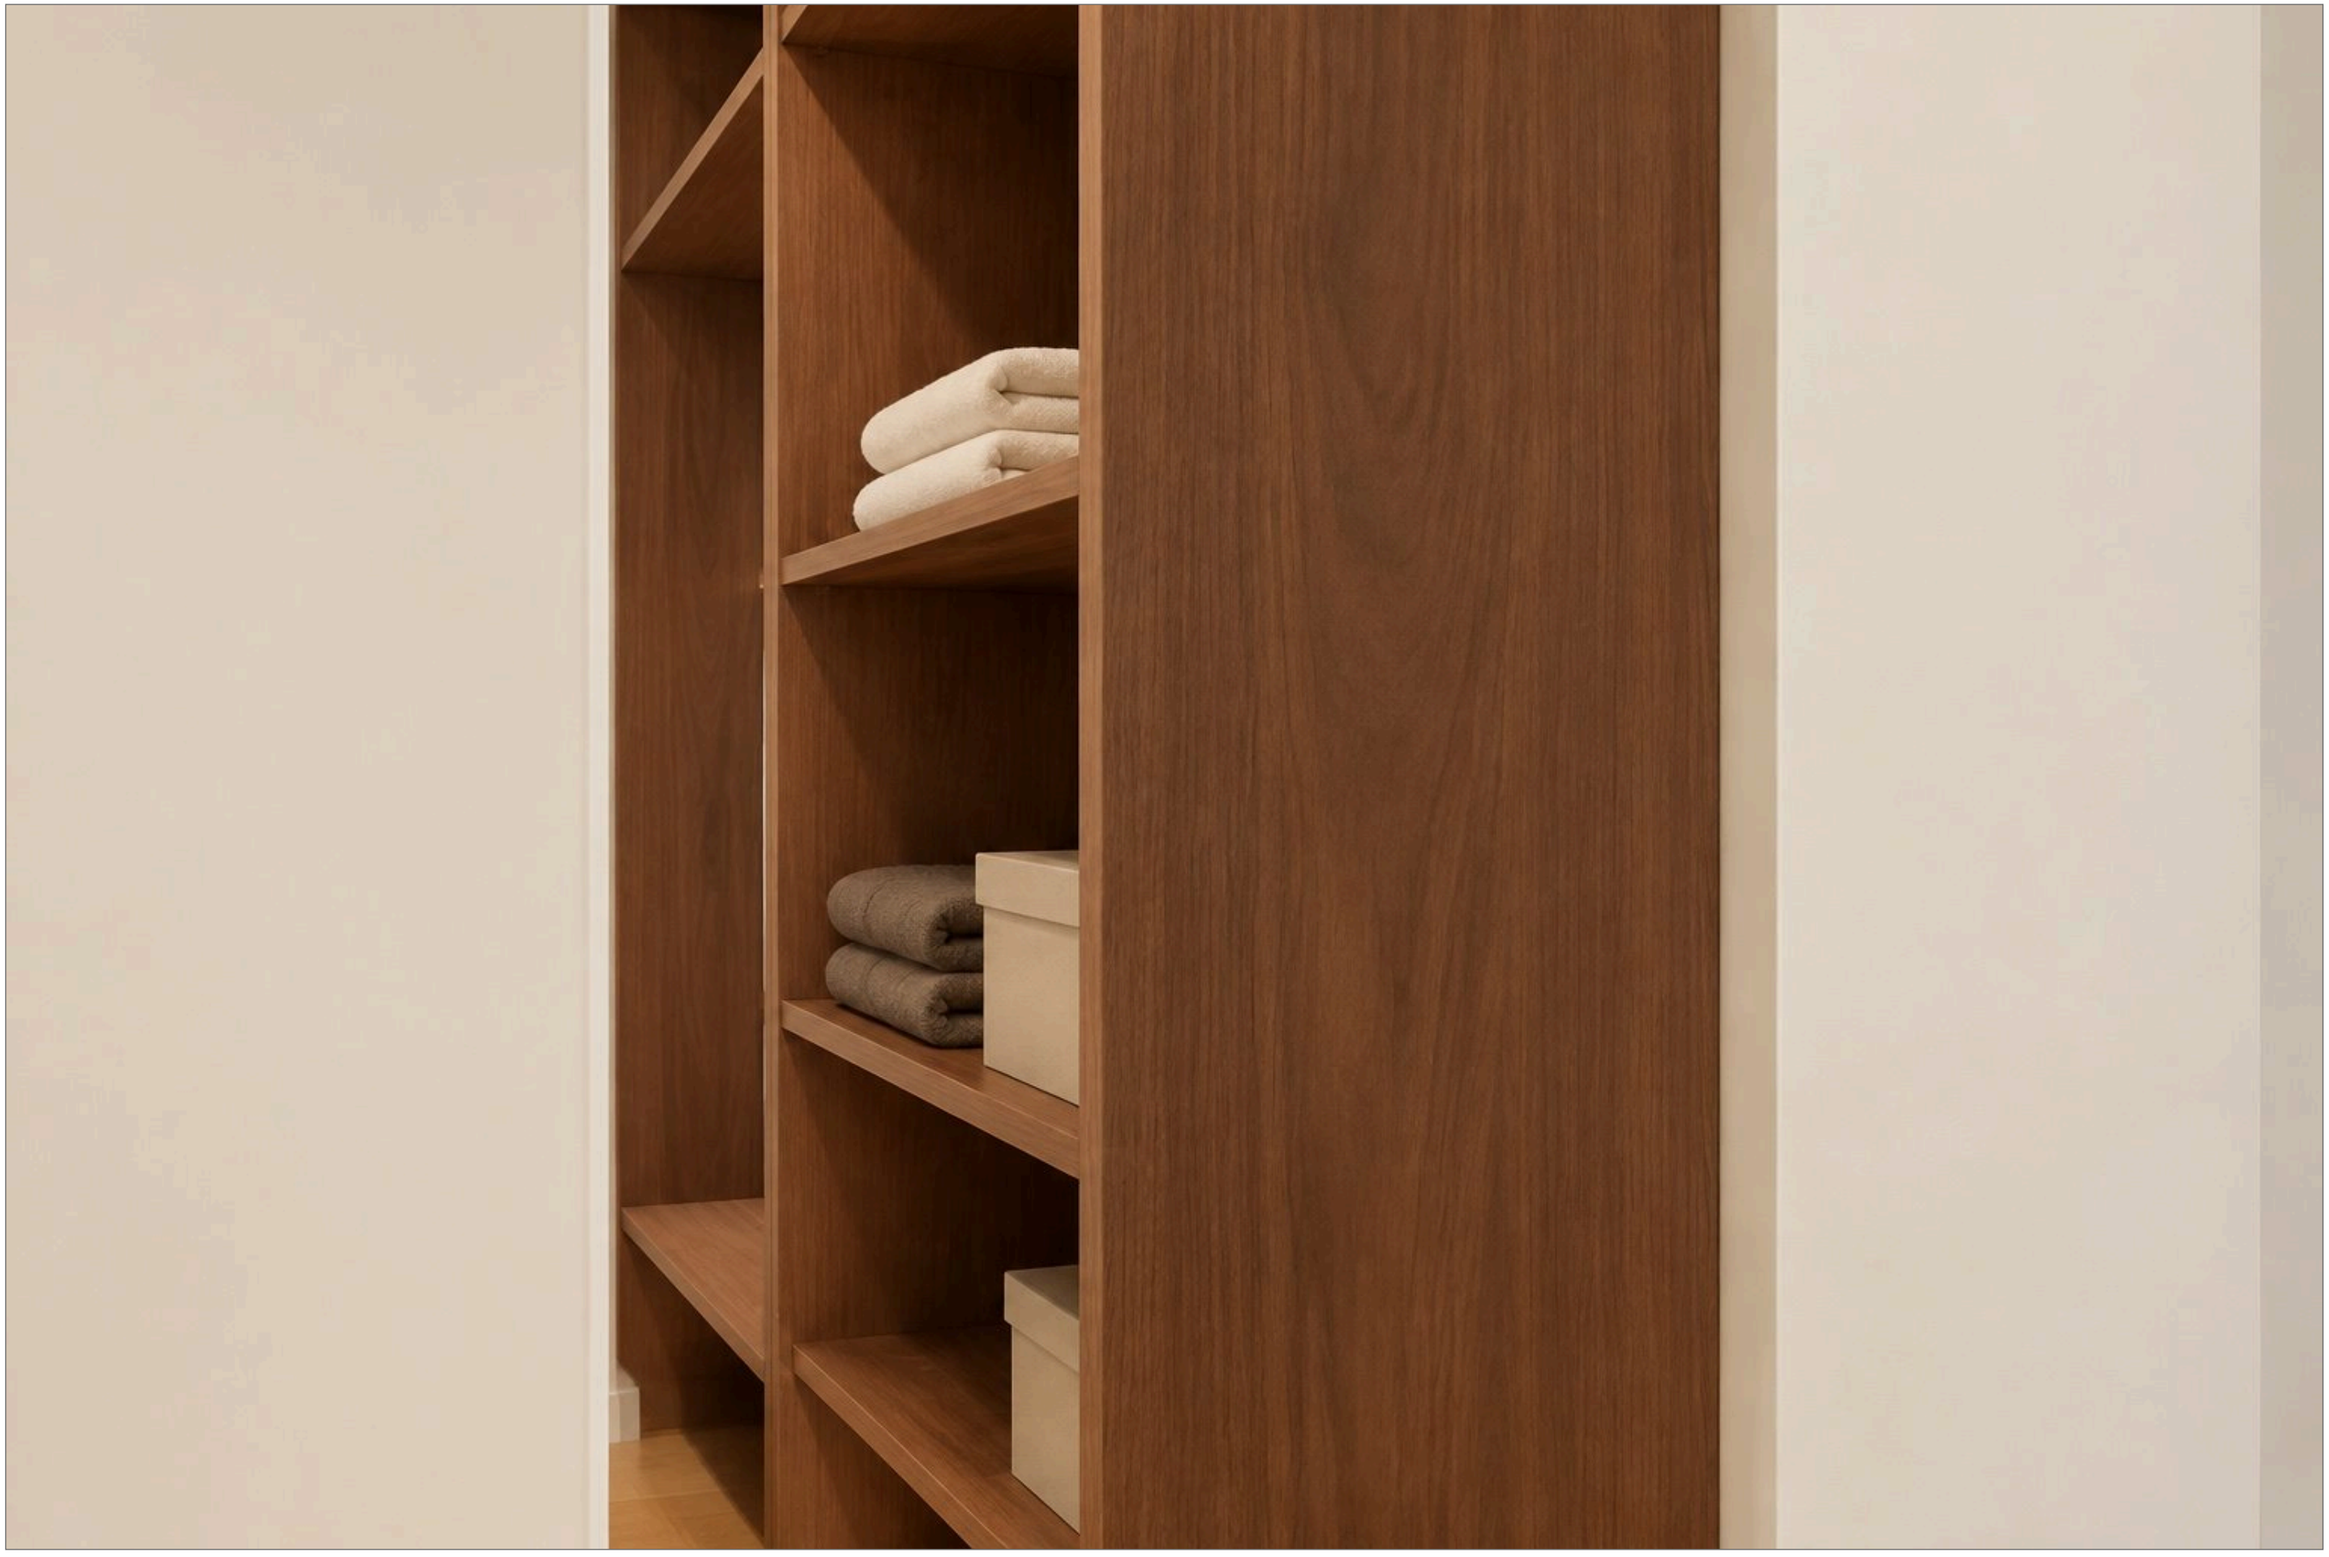

	Лист	№ док.	Подпись	Дата	Проект: Квартира 103 м²			
Дизайнер	Кырлан А.С.			14.11.26	Визуализация кладовой	Стадия	Лист	Листов
Проверил						П	6	129
Н. контр.								
Утв.								



	Лист	№ док.	Подпись	Дата	Проект: Квартира 103 м²			
Дизайнер	Кырлан А.С.			14.11.26				
Проверил					Визуализация: Гостиная-столовая	Стадия	Лист	Листов
Н. контр.								
Утв.						П	7	129

выпуск 14.11.2026 № 32d0256903 · стр. 7 из 129



	Лист	№ док.	Подпись	Дата	Проект: Квартира 103 м²			
Дизайнер	Кырлан А.С.			14.11.26				
Проверил					Визуализация: Прихожая-холл	Стадия	Лист	Листов
Н. контр.								
Утв.						П	8	129



	Лист	№ док.	Подпись	Дата
Дизайнер	Кырлан А.С.			14.11.26
Проверил				
Н. контр.				
Утв.				

Проект: Квартира 103 м²

Визуализация кухни	Стадия	Лист	Листов
	П	9	129



	Лист	№ док.	Подпись	Дата
Дизайнер	Кырлан А.С.			14.11.26
Проверил				
Н. контр.				
Утв.				

Проект: Квартира 103 м²

Визуализация кухни	Стадия	Лист	Листов
	П	10	129

выпуск 14.11.2026 № 32d0256903 · стр. 10 из 129




	Лист	№ док.	Подпись	Дата	Проект: Квартира 103 м²			
Дизайнер	Кырлан А.С.			14.11.26	Визуализация ванной	Стадия	Лист	Листов
Проверил						П	11	129
Н. контр.								
Утв.								



	Лист	№ док.	Подпись	Дата	Проект: Квартира 103 м²			
Дизайнер	Кырлан А.С.			14.11.26				
Проверил					Визуализация ванной	Стадия	Лист	Листов
Н. контр.								
Утв.						П	12	129

выпуск 14.11.2026 № 32d0256903 · стр. 12 из 129

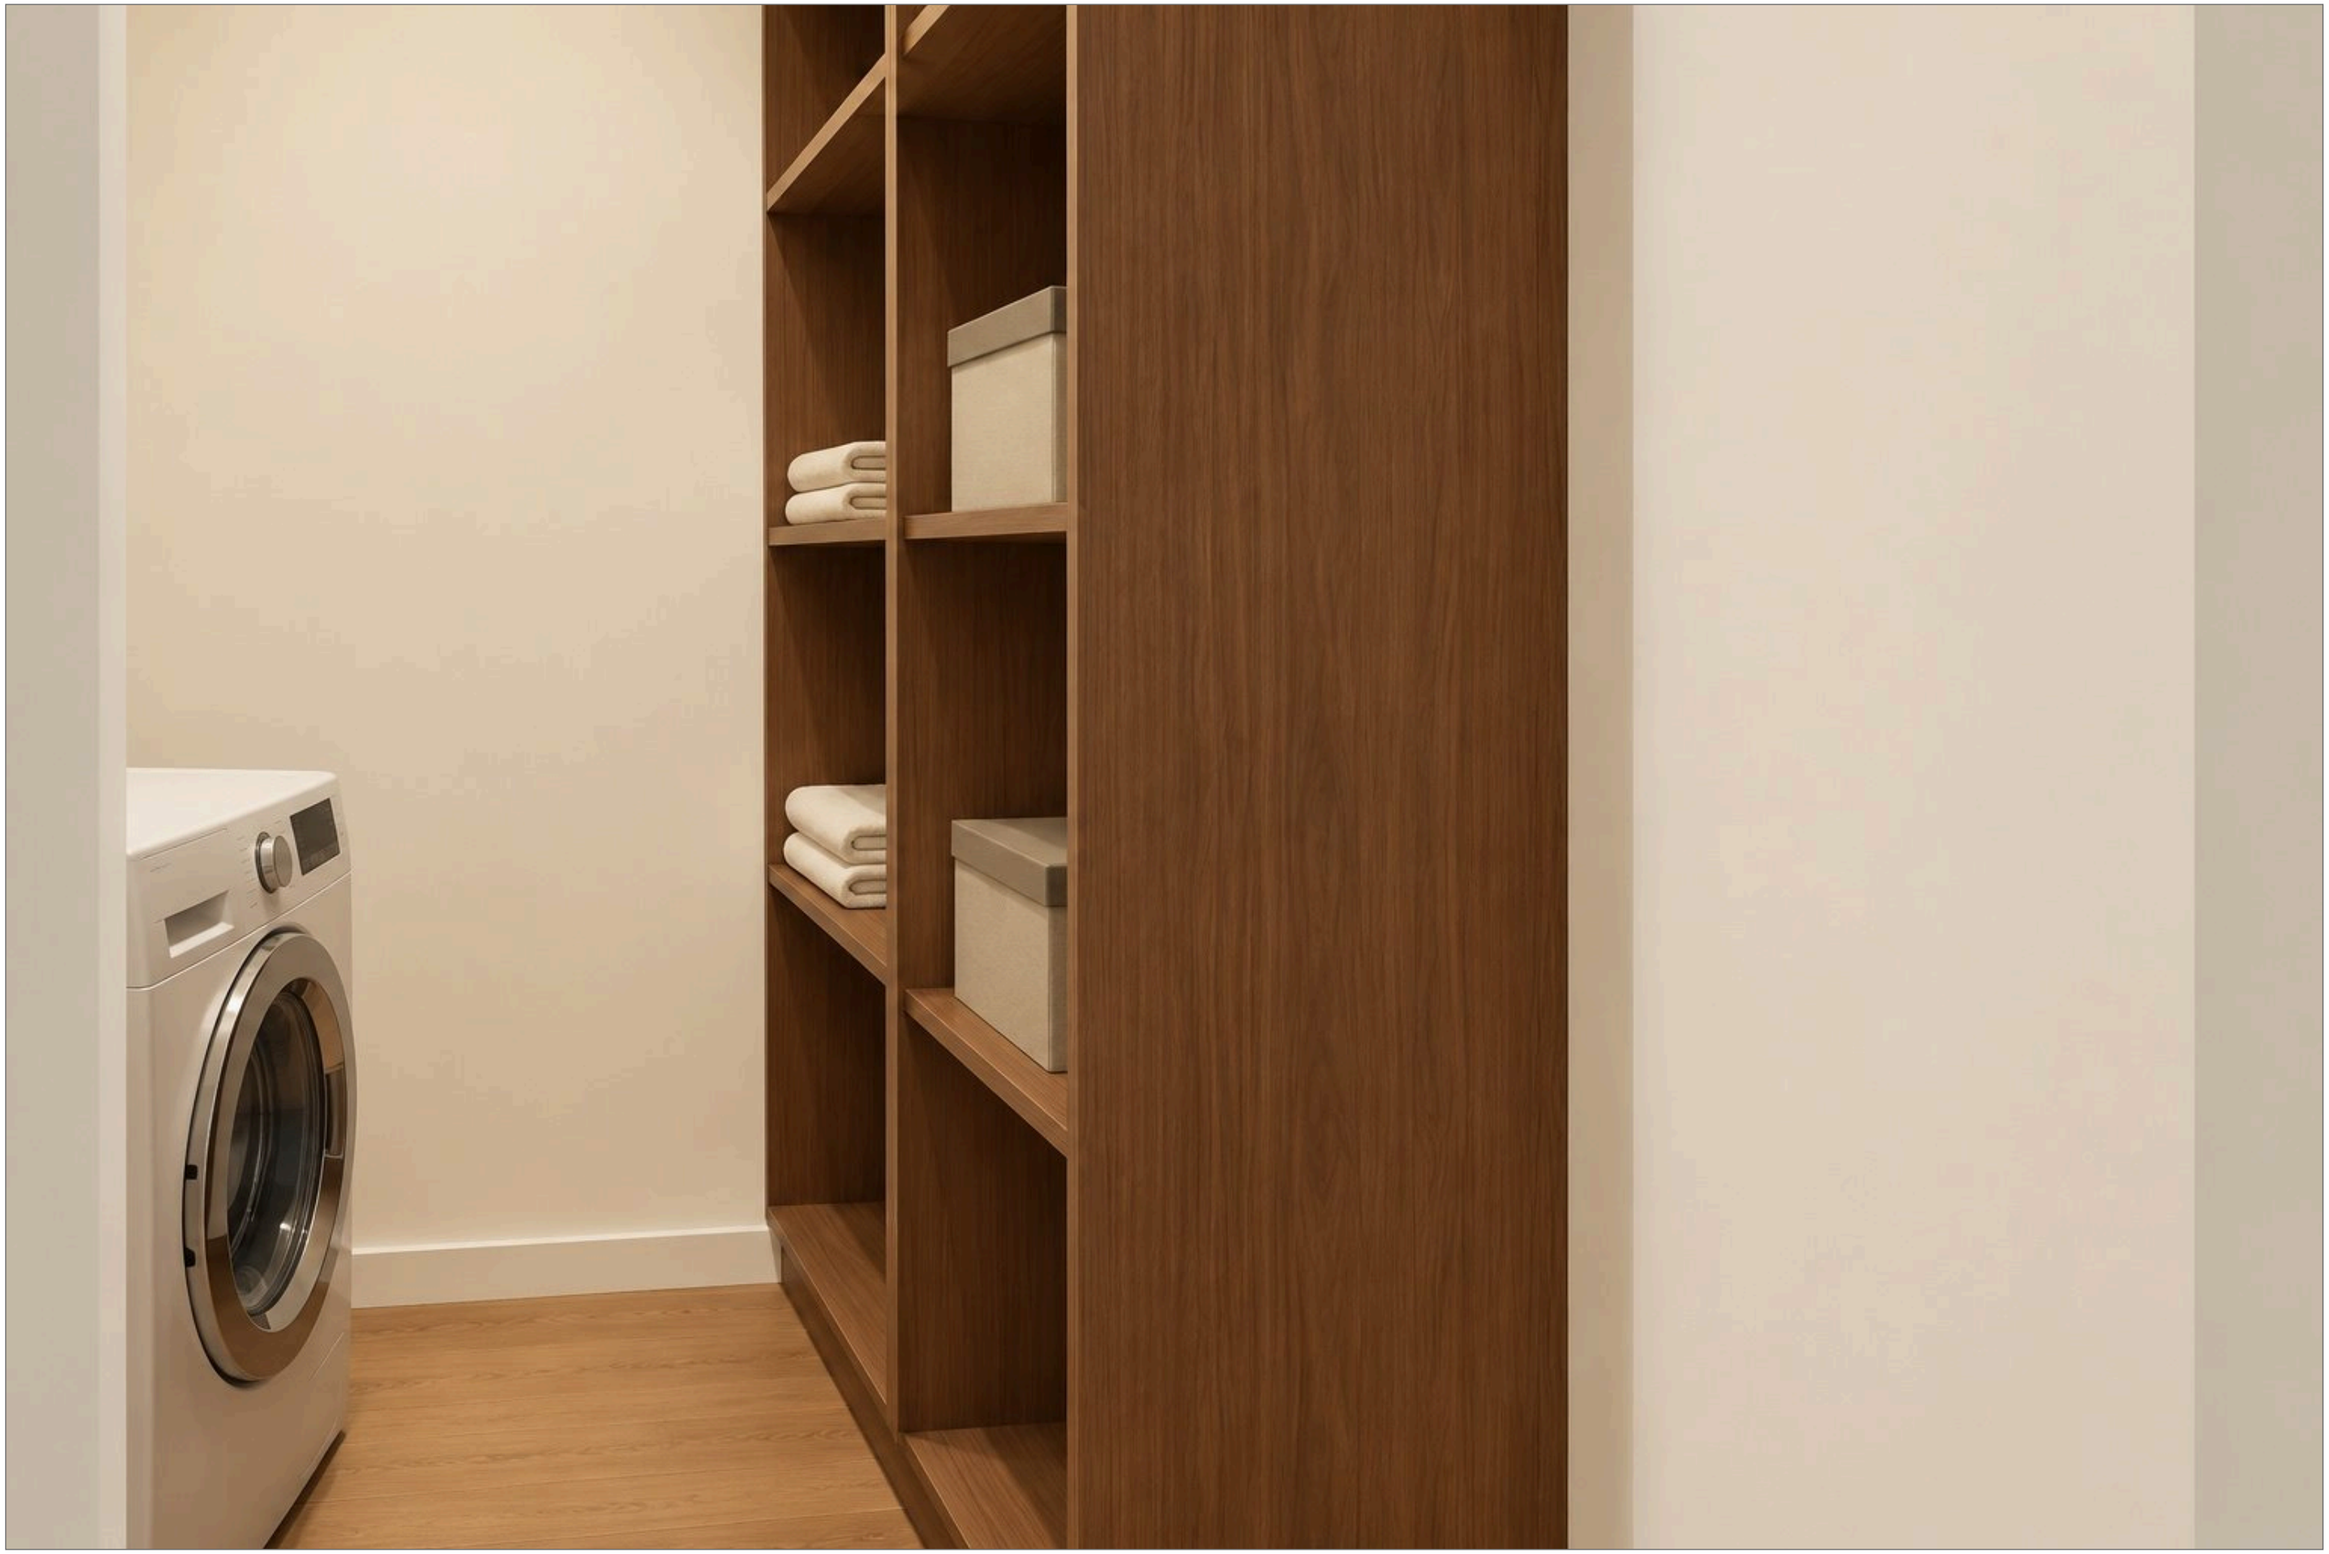

	Лист	№ док.	Подпись	Дата
Дизайнер	Кырлан А.С.			14.11.26
Проверил				
Н. контр.				
Утв.				

Проект: Квартира 103 м²

Визуализация постирочной	Стадия	Лист	Листов
	П	13	129



	Лист	№ док.	Подпись	Дата	Проект: Квартира 103 м²			
Дизайнер	Кырлан А.С.			14.11.26				
Проверил					Визуализация: Спальня 2	Стадия	Лист	Листов
Н. контр.								
Утв.						П	14	129

выпуск 14.11.2026 № 32d0256903 · стр. 14 из 129




	Лист	№ док.	Подпись	Дата	Проект: Квартира 103 м²			
Дизайнер	Кырлан А.С.			14.11.26				
Проверил					Визуализация: Спальня 2	Стадия	Лист	Листов
Н. контр.								
Утв.						П	15	129



	Лист	№ док.	Подпись	Дата	Проект: Квартира 103 м²			
Дизайнер	Кырлан А.С.			14.11.26	Визуализация: Спальня 2	Стадия	Лист	Листов
Проверил						П	16	129
Н. контр.								
Утв.								

выпуск 14.11.2026 № 32d0256903 · стр. 16 из 129

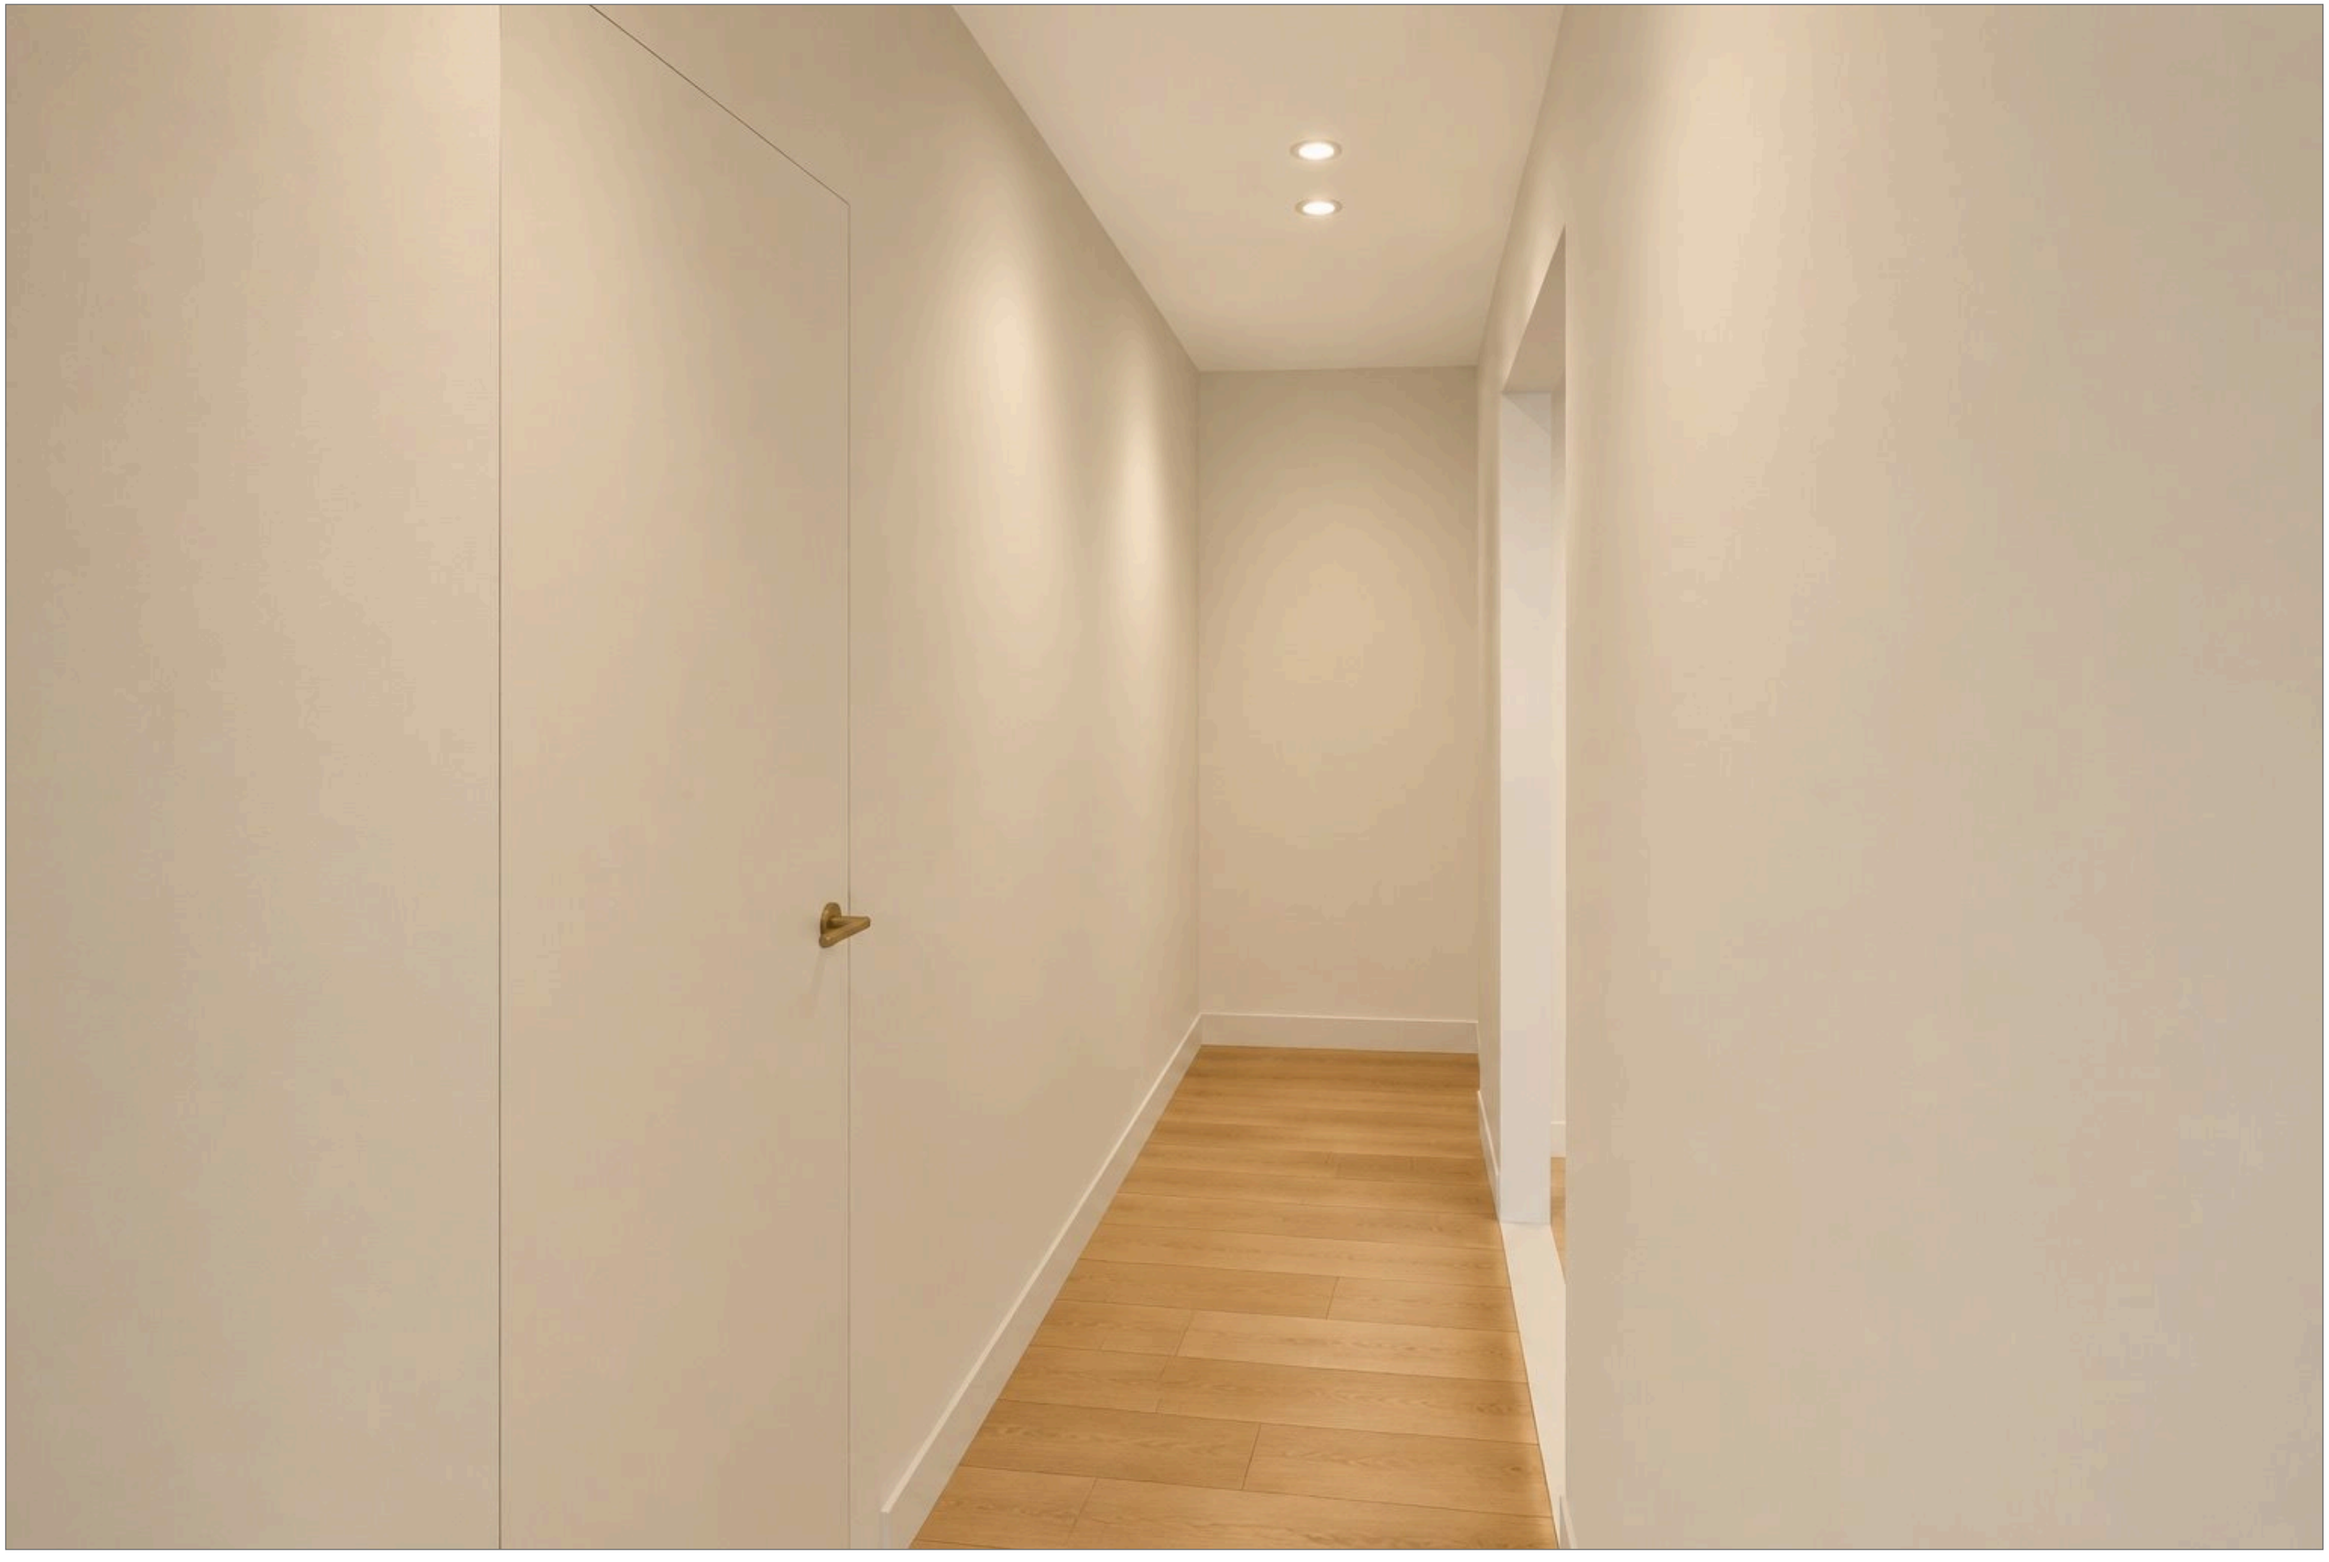

	Лист	№ док.	Подпись	Дата	Проект: Квартира 103 м²			
Дизайнер	Кырлан А.С.			14.11.26				
Проверил					Визуализация коридора	Стадия	Лист	Листов
Н. контр.								
Утв.						П	17	129

выпуск 14.11.2026 № 32d0256903 · стр. 17 из 129



	Лист	№ док.	Подпись	Дата	Проект: Квартира 103 м²			
Дизайнер	Кырлан А.С.			14.11.26				
Проверил					Визуализация: Спальня мастер	Стадия	Лист	Листов
Н. контр.								
Утв.						П	18	129

выпуск 14.11.2026 № 32d0256903 · стр. 18 из 129



	Лист	№ док.	Подпись	Дата
Дизайнер	Кырлан А.С.			14.11.26
Проверил				
Н. контр.				
Утв.				

Проект: Квартира 103 м²

Визуализация: Спальня мастер	Стадия	Лист	Листов
	П	19	129

выпуск 14.11.2026 № 32d0256903 · стр. 19 из 129



	Лист	№ док.	Подпись	Дата	Проект: Квартира 103 м²			
Дизайнер	Кырлан А.С.			14.11.26				
Проверил					Визуализация: Спальня мастер	Стадия	Лист	Листов
Н. контр.								
Утв.						П	20	129

выпуск 14.11.2026 № 32d0256903 · стр. 20 из 129



	Лист	№ док.	Подпись	Дата	Проект: Квартира 103 м²			
Дизайнер	Кырлан А.С.			14.11.26				
Проверил					Визуализация: Ванная мастер	Стадия	Лист	Листов
Н. контр.						П	21	129
Утв.								

выпуск 14.11.2026 № 32d0256903 · стр. 21 из 129

Список листов

Лист	Наименование
1	Титульный лист
2	Ваш проект на одной странице
3	Визуализация: Кабинет-библиотека
4	Визуализация: Кабинет-библиотека
5	Визуализация: Кабинет-библиотека
6	Визуализация кладовой
7	Визуализация: Гостиная-столовая
8	Визуализация: Прихожая-холл
9	Визуализация кухни
10	Визуализация кухни
11	Визуализация ванной
12	Визуализация ванной
13	Визуализация постирочной
14	Визуализация: Спальня 2
15	Визуализация: Спальня 2
16	Визуализация: Спальня 2
17	Визуализация коридора
18	Визуализация: Спальня мастер
19	Визуализация: Спальня мастер
20	Визуализация: Спальня мастер
21	Визуализация: Ванная мастер
22	Список листов
23	Список листов
24	Как читать альбом
25	План планировки от заказчика
26	План монтажный
27	Кухня (пом. 5). Монтажная схема
28	Кухня (пом. 5). Монтажная схема
29	Шкафы. Монтажная схема
30	Карта покрытий стен
31	Колерная карта
32	Колерная карта
33	План размещения мебели и оборудования
34	Спецификация мебели и оборудования
35	Спецификация мебели и оборудования (продолжение)
36	Спецификация мебели и оборудования (продолжение)
37	Ведомости изделий, техники и фурнитуры
38	План выводов сантехники
39	Схема разводки водопровода и канализации
40	Аксонометрическая схема В1 (холодное водоснабжение)
41	Аксонометрическая схема Т3 (горячее водоснабжение)
42	Аксонометрическая схема К1 (канализация)
43	Развёртки мокрых зон: выводы ВК. Кухня
44	Развёртки мокрых зон: выводы ВК. Ванная
45	Развёртки мокрых зон: выводы ВК. Постирочная
46	Развёртки мокрых зон: выводы ВК. Ванная мастер
47	Спецификация сантехнического оборудования
48	Раскладка плитки. Ванная. Развёртки стен
49	Раскладка плитки. Ванная мастер. Развёртки стен
50	План размещения дверей
51	Ведомость заполнения проёмов
52	План потолков
53	Разрезы и узлы потолков
54	Разрезы и узлы потолков (продолжение)
55	Сечения потолков М 1:10
56	Однолинейная схема щита
57	Таблица нагрузок щита
58	План принципиальных трасс
59	План розеток и электровыводов
60	План слаботочных сетей
61	План освещения
62	Техническое задание на подбор светильников
63	Управление светильниками
64	План вентиляции
65	План отопления

	Лист	№ док.	Подпись	Дата	Проект: Квартира 103 м²			
Дизайнер	Кырлан А.С.			14.11.26	Список листов	Стадия	Лист	Листов
Проверил						П	22	129
Н. контр.								
Утв.								

выпуск 14.11.2026 № 32d0256903 · стр. 22 из 129

Список листов (продолжение)

Лист	Наименование
66	План покрытий пола
67	Раскладка плитки. Планы полов
68	Раскладка плитки. Прихожая-холл
69	Развёртка стены А. Кабинет-библиотека (пом. 1)
70	Развёртка стены Б. Кабинет-библиотека (пом. 1)
71	Развёртка стены В. Кабинет-библиотека (пом. 1)
72	Развёртка стены Г. Кабинет-библиотека (пом. 1)
73	Развёртки стен. Кладовая (пом. 2)
74	Развёртка стены А. Гостиная-столовая (пом. 3)
75	Развёртка стены Б. Гостиная-столовая (пом. 3)
76	Развёртка стены В. Гостиная-столовая (пом. 3)
77	Развёртка стены Г. Гостиная-столовая (пом. 3)
78	Развёртка стены А. Прихожая-холл (пом. 4)
79	Развёртка стены Б. Прихожая-холл (пом. 4)
80	Развёртка стены В. Прихожая-холл (пом. 4)
81	Развёртка стены Г. Прихожая-холл (пом. 4)
82	Развёртка стены Б. Кухня (пом. 5), кухонный фронт
83	Развёртка стены В. Кухня (пом. 5), кухонный фронт
84	Развёртки стен А, Г. Кухня (пом. 5)
85	Развёртки стен А, В. Ванная (пом. 6)
86	Развёртка стены Б. Ванная (пом. 6)
87	Развёртка стены Г. Ванная (пом. 6)
88	Развёртки стен А, Б. Постирочная (пом. 7)
89	Развёртки стен В, Г. Постирочная (пом. 7)
90	Развёртка стены А. Спальня 2 (пом. 8)
91	Развёртка стены Б. Спальня 2 (пом. 8)
92	Развёртка стены В. Спальня 2 (пом. 8)
93	Развёртка стены Г. Спальня 2 (пом. 8)
94	Развёртки стен А, В. Коридор (пом. 9)
95	Развёртка стены Б. Коридор (пом. 9)
96	Развёртка стены А. Спальня мастер (пом. 10)
97	Развёртка стены Б. Спальня мастер (пом. 10)
98	Развёртка стены В. Спальня мастер (пом. 10)
99	Развёртка стены Г1. Спальня мастер (пом. 10)
100	Развёртка стены Г2. Спальня мастер (пом. 10)
101	Развёртки стен А, Б. Ванная мастер (пом. 11)
102	Развёртки стен В, Г. Ванная мастер (пом. 11)
103	Открытые вопросы, принятые допущения и конфликты. Лист 1 из 2
104	Открытые вопросы, принятые допущения и конфликты. Лист 2 из 2
Д1	Система хранения М-05
Д2	Шкаф-купе М-11
Д3	Система хранения М-22
Д4	Шкаф распашной М-24
Д5	Шкаф распашной М-29
Д6	Кухня (пом. 5). Развёртка гарнитура
Д7	Кухня (пом. 5). Развёртка гарнитура
С1	Ведомость отделки помещений. Лист 1 из 2
С2	Ведомость отделки помещений. Лист 2 из 2
С3	Спецификация отделочных материалов
С4	Список покупок
С5	Список покупок (окончание)
С6	Смета проекта: этапы, помещения, итог
С7	Смета проекта: этапы, помещения, итог (продолжение)
С8	Смета проекта: этапы, помещения, итог (окончание)
С9	Смета материалов с ценами
С10	Смета материалов с ценами (продолжение)
С11	Смета материалов с ценами (продолжение)
С12	Смета материалов с ценами (окончание)
С13	Узлы
С14	Календарный график работ и закупок
С15	Чек-лист приёмки по этапам. Лист 1 из 3
С16	Чек-лист приёмки по этапам. Лист 2 из 3
С17	Чек-лист приёмки по этапам. Лист 3 из 3
С18	Лист → мастер

Общие указания

1. Размеры даны в мм от чистовых поверхностей стен: слой штукатурки 20 мм по блоку и 5 мм шпаклёвки по ГКЛ учтён. Перед заказом встроенной мебели — контрольный обмер после штукатурки.
2. Привязки мебели — от стен и углов помещения, а не от другой мебели.
3. Розетки, выводы и выключатели под мебель — см. лист 59 «План розеток и электровыводов»; сантехприборы и выводы воды — лист 38.
4. План расстановки не является документацией для изготовления мебели: изделия — по чертежам мебельщика; покупную мебель заменять только на изделия не больше габарита из спецификации (лист 34).
5. Встроенная мебель «стена в стену» — с зазором 10 мм с каждой стороны или с компенсаторами.
6. Развёртки — вид на стену изнутри помещения, по часовой стрелке; расположение стен на схеме листа развёртки; размеры — в мм по чистовым поверхностям; отметки — в м от ±0,000; высоты Н — от чистого пола помещения до оси изделия, у декора — до центра.
7. Красная цепочка — привязки электроточек и выводов по осям от угла чистовых стен; высота Н — у знака, от чистого пола до оси; высоты мебели, проёмов и границ отделки колонкой отметок слева. У знака — короткая марка; назначение, группа щита, высота и привязка каждой точки и вывода — в «Ведомости точек и выводов» под видами (каждая точка — строка).
8. У знака электроточки: марка (Р — розетка, S — выключатель, Св — светильник, ЭВ вывод кабеля), ×N — число постов в рамке, гр. — группа щита, Н — высота оси от чистого пола, мм; группы по клавишам выключателя — на листе выключателей.
9. Схема мебели, приборов и декора не является технической документацией для производства мебели; габариты — по паспортам изделий.
10. Марки позиций: М-NN — мебель, ОБ-NN — оборудование, С-NN — сантехника; О-N отделка (ведомость отделочных материалов, серия С).
11. Размеры мебели и изделий на заказ уточнить по месту после отделочных работ.

	Лист	№ док.	Подпись	Дата
Дизайнер	Кырлан А.С.			14.11.26
Проверил				
Н. контр.				
Утв.				

Проект: Квартира 103 м²

Список листов	Стадия	Лист	Листов
	П	23	129

выпуск 14.11.2026 № 32d0256903 · стр. 23 из 129

Что в альбоме

Альбом — дизайн-проект с рабочими чертежами для ремонта. Листы идут в порядке работ: титул и вводные, реестр открытых вопросов и решений, планы (обмер, монтаж стен, мебель, двери, потолки, полы), инженерия (сантехника, электрика, вентиляция и отопление), развёртки стен с визуализациями помещений, чертежи мебели, ведомости материалов и узлы.

Вам как заказчику — титул, эта вводная, «Ваш проект на одной странице», реестр вопросов, план мебели, визуализации и развёртки, ведомости мебели и материалов. Подрядчику — всё остальное: монтажные планы, привязки выводов и розеток, узлы, ведомости объёмов.

Знаки на листах

Без знака — решение утверждено или подтверждено обмером.

Что проверить до ремонта

1. Розетки у кровати и рабочего места: хватает ли их с каждой стороны кровати и над столом (план розеток — лист 59).

2. Выводы под технику — варочная панель, духовка, посудомойка, стиральная машина, бойлер: совпадают ли с выбранными моделями (листы 34, 35, 36, 59).

3. Высоты розеток, выключателей и выводов даны от чистого пола: если мебель или техника будут другими — скажите до штробления стен.

Номера записей

К-N — открытый вопрос: чего не хватает или что выбрать (варианты и рекомендация — в тексте). Пока ответа нет, действует строка «если решения нет».

Кф-N — конфликт между разделами (например, мебель и радиатор в одном месте); закрывается решением, которое записывается как ИЗ-N.

ИЗ-N — изменение проекта: что было, что стало и кто утвердил. Изменение без подписи предложение.

Все записи — на листе реестра сразу после вводных; на других листах на них стоят ссылки.

Почему альбом предварительный

Обмера на объекте не было: размеры взяты с плана заказчика. Технические условия (мощность, вода, вентиляция дома) не получены, часть решений ждёт вашего ответа. Пока в реестре есть открытые вопросы, альбом предварительный — пометка в штампе снимается закрытием вопросов, а не стиранием.

Правку к любому листу можно оставить по кнопке «Правка к листу» или на сайте студии: дизайн-студия-квартир.рф — укажите номер листа и что изменить.

3 круга правок входят в цену; условия — в договоре и на странице вашего заказа на сайте студии.


Шифр проекта ГД-2026-009-АИ

	Лист	№ док.	Подпись	Дата	Проект: Квартира 103 м²			
Дизайнер	Кырлан А.С.			14.11.26				
Проверил					Как читать альбом	Стадия	Лист	Листов
Н. контр.								
Утв.						П	24	129

выпуск 14.11.2026 № 32d0256903 · стр. 24 из 129

Отметки по высоте

±0,000 чистый пол пом. 1–5, 7–10; отсчёт высот
−0,015 чистый пол пом. 6, 11, ниже на 15 мм
−0,064 верх плиты — расчёт, не замер (задание на обмер)
сущ. пол снимается до плиты; не замерен (задание на обмер)

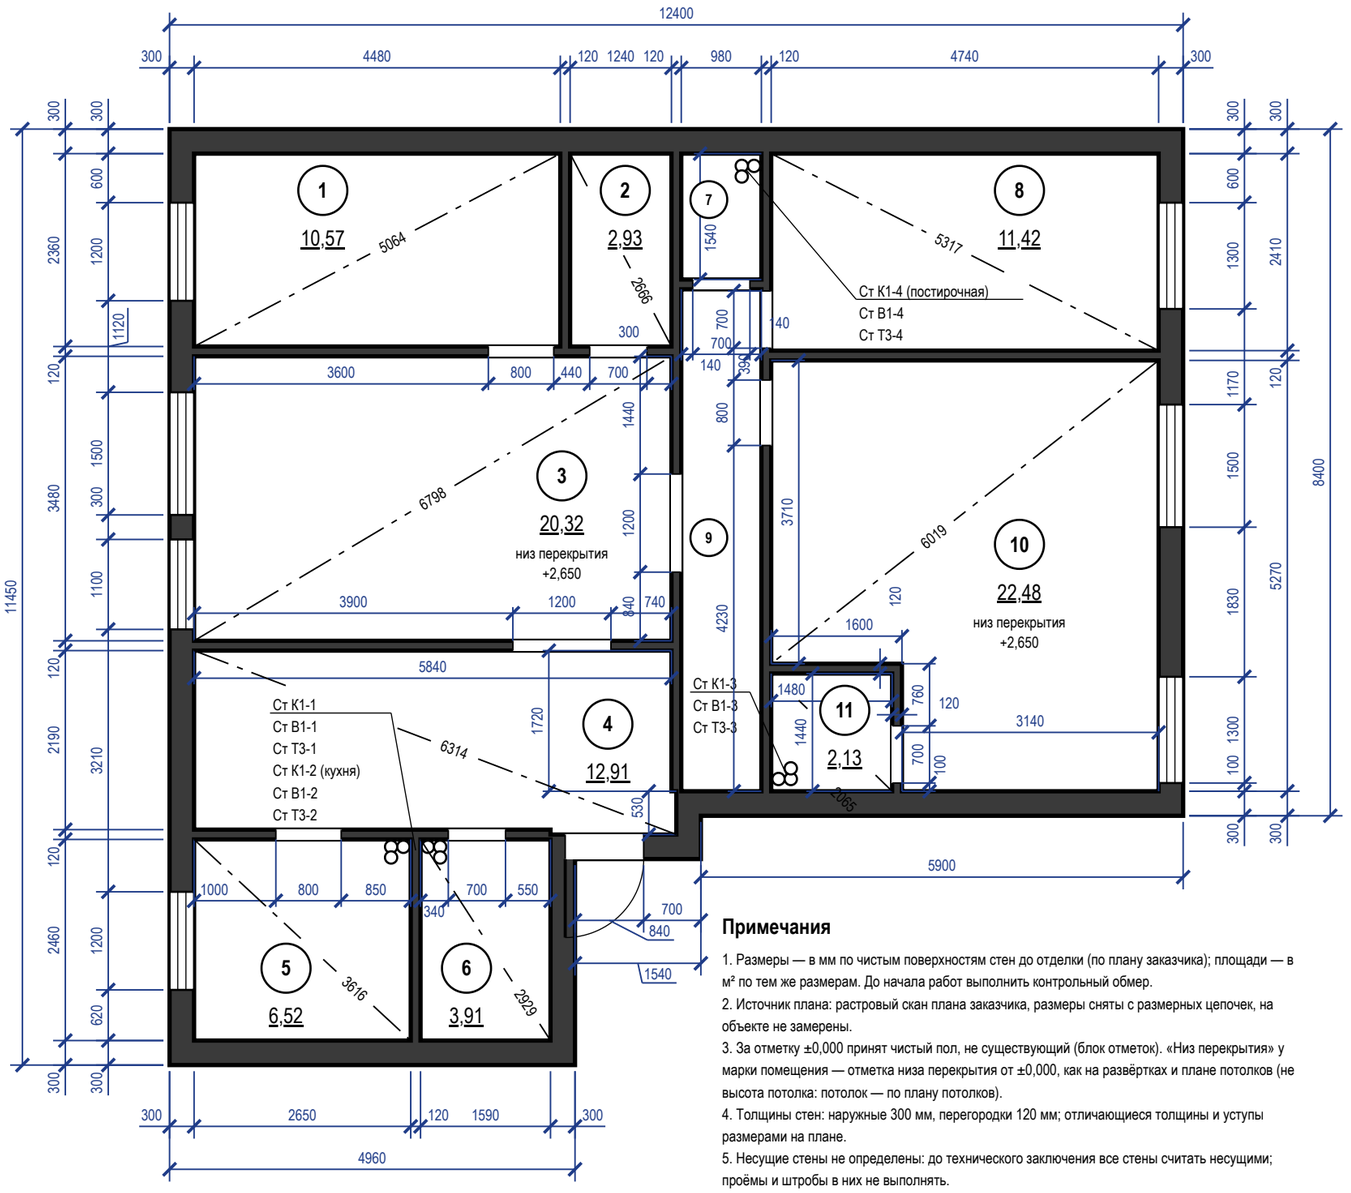

Экспликация помещений

№	Наименование	Площадь, м²
1	Кабинет-библиотека	10,57
2	Кладовая	2,93
3	Гостиная-столовая	20,32
4	Прихожая-холл	12,91
5	Кухня	6,52
6	Ванная	3,91
7	Постирочная	1,51
8	Спальня 2	11,42
9	Коридор	6,02
10	Спальня мастер	22,48
11	Ванная мастер	2,13
	Итого (общая площадь)	**100,72**

Условные обозначения

- существующие стены (сечение)
- окно (рама, остекление)
- проём существующий, без заполнения (откосы)
- стояк: К1 — канализация, В1 — ХВС, Т3 — ГВС
- диагональ помещения — контроль прямоугольности
- (1) номер помещения, площадь м²

Примечания

1. Размеры — в мм по чистым поверхностям стен до отделки (по плану заказчика); площади — в м² по тем же размерам. До начала работ выполнить контрольный обмер.
2. Источник плана: растровый скан плана заказчика, размеры сняты с размерных цепочек, на объекте не замерены.
3. За отметку ±0,000 принят чистый пол, не существующий (блок отметок). «Низ перекрытия» у марки помещения — отметка низа перекрытия от ±0,000, как на развёртках и плане потолков (не высота потолка: потолок — по плану потолков).
4. Толщины стен: наружные 300 мм, перегородки 120 мм; отличающиеся толщины и уступы размерами на плане.
5. Несущие стены не определены: до технического заключения все стены считать несущими; проёмы и штробы в них не выполнять.
6. Дверные проёмы показаны без заполнения (двери — лист 51); высота дверных проёмов 2100 мм, проёмов без двери 2100 мм; низ окон (подоконник) 720, 735, 763, 783, 825 мм от чистого пола, высота окон 1560, 1550, 1552, 1548 мм.
7. Диагонали — контрольные размеры; расхождение более 5 мм подписать на плане как перекос.
8. Размеры проверить на месте до начала работ; расхождение контрольных промеров ≤ 2 %.
9. Размеры короче 1 мм на листе цепочкой не показаны (две выносные линии на таком расстоянии сливаются): пом. 9, стена Б — 20 мм от угла до проёма.


	Лист	№ док.	Подпись	Дата
Дизайнер	Кырлан А.С.			14.11.26
Проверил				
Н. контр.				
Утв.				

Проект: Квартира 103 м² — **М 1:75**

План планировки от заказчика

Стадия	Лист	Листов
П	25	129

выпуск 14.11.2026 № 32d0256903 · стр. 25 из 129

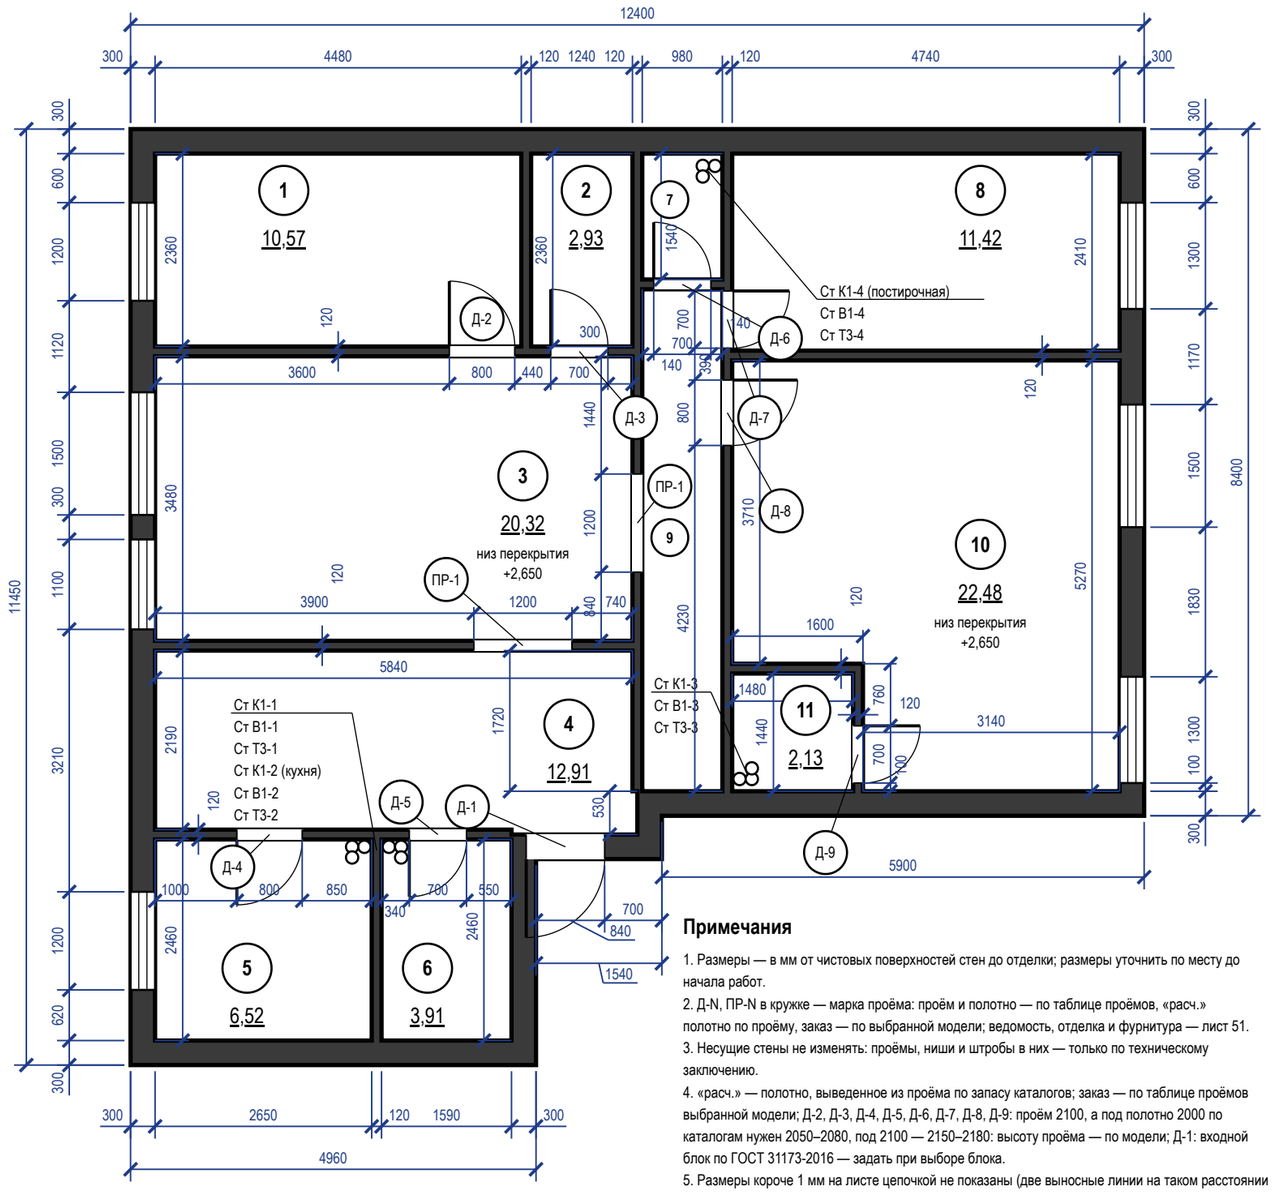

Примечания

1. Размеры — в мм от чистовых поверхностей стен до отделки; размеры уточнить по месту до начала работ.
2. Д-N, ПР-N в кружке — марка проёма: проём и полотно — по таблице проёмов, «расч.» полотно по проёму, заказ — по выбранной модели; ведомость, отделка и фурнитура — лист 51.
3. Несущие стены не изменять: проёмы, ниши и штробы в них — только по техническому заключению.
4. «расч.» — полотно, выведенное из проёма по запасу каталогов; заказ — по таблице проёмов выбранной модели; Д-2, Д-3, Д-4, Д-5, Д-6, Д-7, Д-8, Д-9: проём 2100, а под полотно 2000 по каталогам нужен 2050–2080, под 2100 — 2150–2180: высоту проёма — по модели; Д-1: входной блок по ГОСТ 31173-2016 — задать при выборе блока.
5. Размеры короче 1 мм на листе цепочкой не показаны (две выносные линии на таком расстоянии сливаются): пом. 9, стена Б — 20 мм от угла до проёма.

Экспликация помещений

№	Наименование	Площадь, м²
1	Кабинет-библиотека	10,57
2	Кладовая	2,93
3	Гостиная-столовая	20,32
4	Прихожая-холл	12,91
5	Кухня	6,52
6	Ванная	3,91
7	Постирочная	1,51
8	Спальня 2	11,42
9	Коридор	6,02
10	Спальня мастер	22,48
11	Ванная мастер	2,13
	Итого (общая площадь)	**100,72**

Таблица проёмов

Марка	Наименование	Проём ш×в, мм	Полотно (расч.)
Д-1	Дверь входная	960×2100	блок — задать
Д-2	Дверь скрытого монтажа	800×2100	700×2000
Д-3	Дверь скрытого монтажа	700×2100	600×2000
Д-4	Дверь скрытого монтажа	800×2100	700×2000
Д-5	Дверь скрытого монтажа	700×2100	600×2000
Д-6	Дверь скрытого монтажа	700×2100	600×2000
Д-7	Дверь скрытого монтажа	700×2100	600×2000
Д-8	Дверь скрытого монтажа	800×2100	700×2000
Д-9	Дверь скрытого монтажа	700×2100	600×2000
ПР-1	Проём без заполнения	1200×2100	

	Лист	№ док.	Подпись	Дата
Дизайнер	Кырлан А.С.			14.11.26
Проверил				
Н. контр.				
Утв.				


Проект: Квартира 103 м² — **М 1:75**

План монтажный


Стадия	Лист	Листов
П	26	129

выпуск 14.11.2026 № 32d0256903 · стр. 26 из 129

Привязка выводов и крепление модулей (М 1:20)

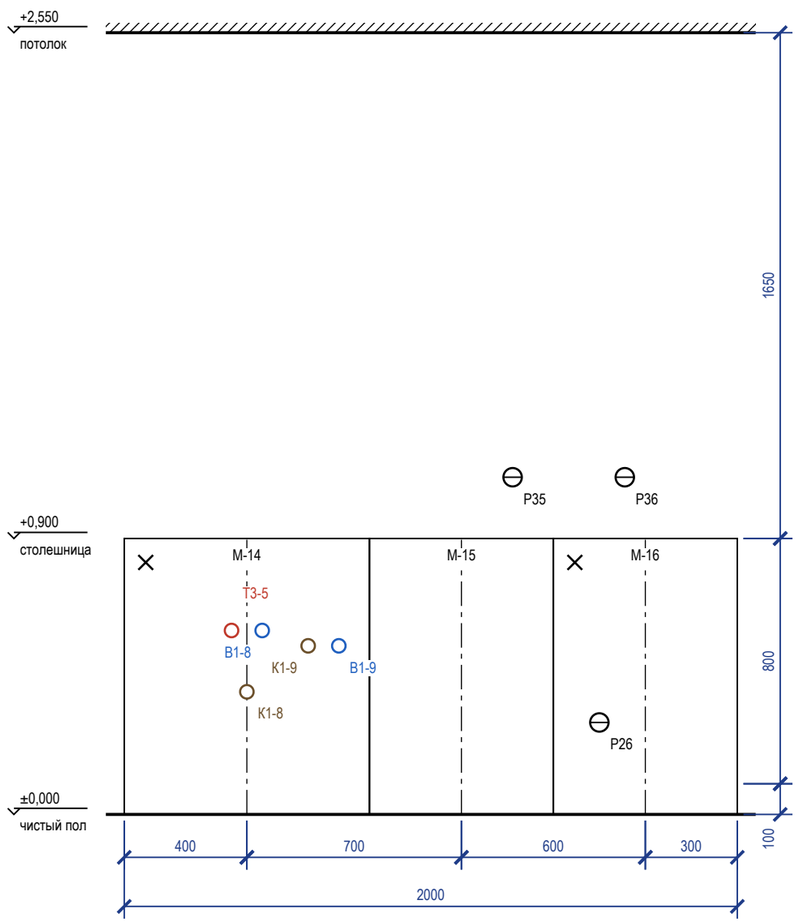

План столешницы (М 1:20)

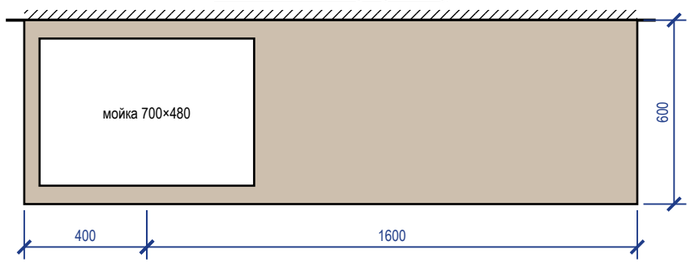

Привязка выводов к осям модулей

Код	Назначение	Модуль	От оси, мм	Н, мм	Размещение
Т3-5	Т3 — межос. 100	М-14	−50	600	в модуле мойки
К1-8	К1 Ø50 — мойка	М-14	0	400	в модуле мойки
В1-8	В1 — межос. 100	М-14	+50	600	в модуле мойки
К1-9	К1 Ø40 — слив ПММ в шкафу мойки	М-14	+200	550	в модуле мойки
В1-9	В1 — кран ПММ в шкафу мойки	М-14	+300	550	в модуле мойки
Р35	розетка ×2 — фартук	М-15	+167	1100	над столешницей (фартук)
Р26	розетка — посудомоечная машина — в соседнем модуле, за ящиком	М-16	−150	300	в соседнем модуле, за ящиком
Р36	розетка ×2 — фартук	М-16	−67	1100	над столешницей (фартук)

Зазоры под отделку

Поверхность	Отделка	Зазор, мм	Учесть
фартук	керамогранит	10	от чернового основания до корпуса навесных и столешницы
стены	окраска	5	под штукатурку и шпаклёвку за пеналом
пол	инженерная доска		цоколь — после укладки пола, опоры ±20 мм

Условные обозначения

- нижний модуль, пенал (контур)
- ось модуля (от неё — привязка вывода)
- анкер / уголок крепления к стене
- розетка на стене
- вывод кабеля к технике
- В1 — вывод воды В1 / Т3, канализации К1


Примечания

1. Выводы — по проекту электрики и ВК; привязка по горизонтали — от оси модуля (плюс — вправо по виду), по высоте — от чистого пола до оси вывода.
2. Пенал — уголки к стене 2 шт. сверху; нижние модули — стяжками между собой и уголком к стене; ряд выставить по уровню опорами цоколя.
3. Розетки над столешницей — не ниже 150 мм над ней и не за корпусом техники; розетка за ПММ, духовым шкафом и холодильником — только в соседнем модуле или в зоне цоколя с доступом.
4. Столешница — вырезы по шаблонам выбранных моделей мойки и варочной панели; торцы у стены — герметик, пристеночный плинтус.


	Лист	№ док.	Подпись	Дата	Проект: Квартира 103 м²			М 1:20
Дизайнер	Кырлан А.С.			14.11.26	Кухня (пом. 5). Монтажная схема	Стадия	Лист	Листов
Проверил						П	27	129
Н. контр.								
Утв.								

выпуск 14.11.2026 № 32d0256903 · стр. 27 из 129

Привязка выводов и крепление модулей (М 1:20)

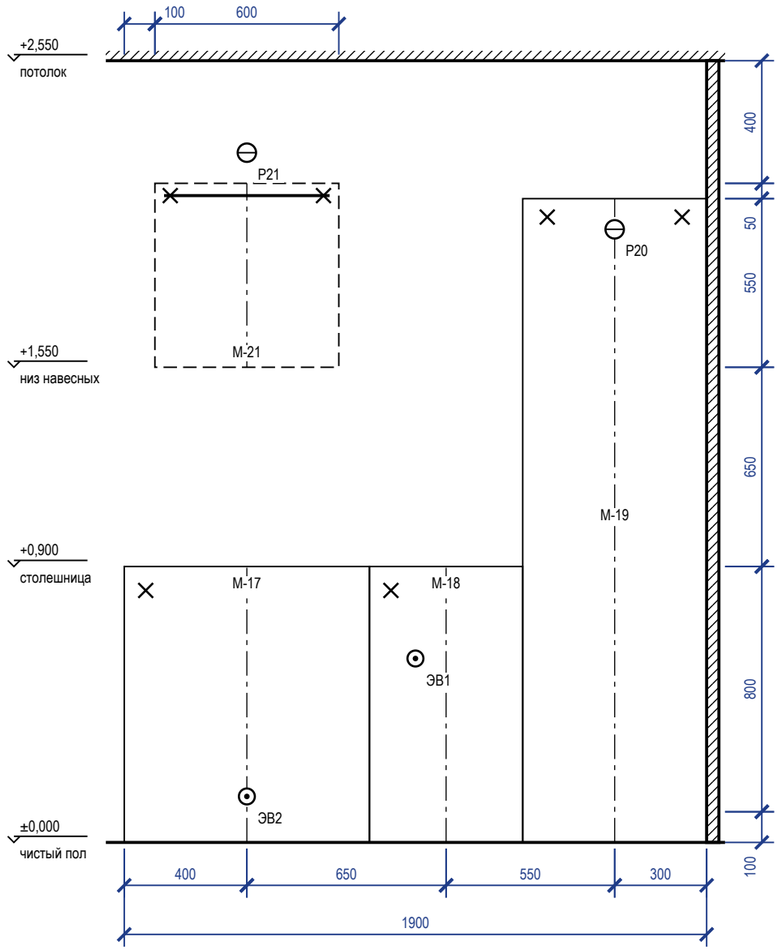

План столешницы (М 1:20)

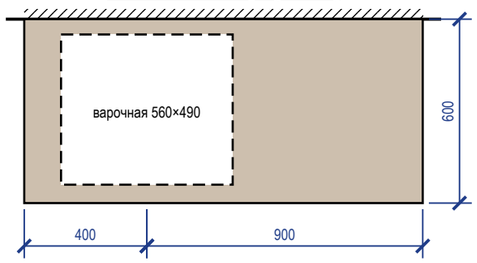

Привязка выводов к осям модулей

Код	Назначение	Модуль	От оси, мм	Н, мм	Размещение
ЭВ2	вывод кабеля — духовой шкаф — в цоколе	М-17	0	150	под духовым шкафом, доступ через ящик
Р21	розетка — вытяжка — над корпусом	М-21	0	2250	в навесном модуле
ЭВ1	вывод кабеля — варочная панель — в соседнем модуле, за ящиком	М-18	−100	600	в соседнем модуле, за ящиком
Р20	розетка — холодильник — над нишей, съёмная панель	М-19	0	2000	над нишей холодильника, съёмная панель

Зазоры под отделку

Поверхность	Отделка	Зазор, мм	Учесть
фартук	керамогранит	10	от чернового основания до корпуса навесных и столешницы
стены	окраска	5	под штукатурку и шпаклёвку за пеналом
пол	инженерная доска		цоколь — после укладки пола, опоры ±20 мм

Условные обозначения


- нижний модуль, пенал (контур)
- невидимый контур: навесной модуль, корпус под столешницей
- ось модуля (от неё — привязка вывода)
- анкер / уголок крепления к стене
- розетка на стене
- вывод кабеля к технике
- B1 — вывод воды В1 / Т3, канализации К1

Примечания


1. Выводы — по проекту электрики и ВК; привязка по горизонтали — от оси модуля (плюс — вправо по виду), по высоте — от чистого пола до оси вывода.
2. Пенал — уголки к стене 2 шт. сверху; нижние модули — стяжками между собой и уголком к стене; ряд выставить по уровню опорами цоколя.
3. Розетки над столешницей — не ниже 150 мм над ней и не за корпусом техники; розетка за ПММ, духовым шкафом и холодильником — только в соседнем модуле или в зоне цоколя с доступом.
4. Столешница — вырезы по шаблонам выбранных моделей мойки и варочной панели; торцы у стены — герметик, пристеночный плинтус.

	Лист	№ док.	Подпись	Дата	Проект: Квартира 103 м²			М 1:20
Дизайнер	Кырлан А.С.			14.11.26	Кухня (пом. 5). Монтажная схема	Стадия	Лист	Листов
Проверил						П	28	129
Н. контр.								
Утв.								


Система хранения М-05 (пом. 2) (М 1:50)

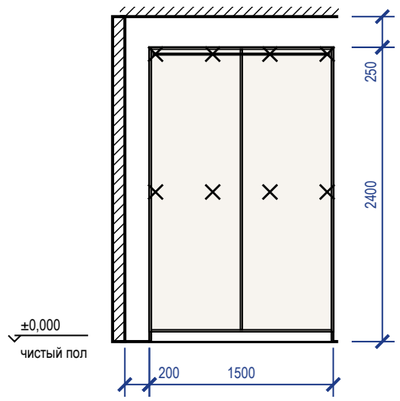


Шкаф-купе М-11 (пом. 4) (М 1:50)

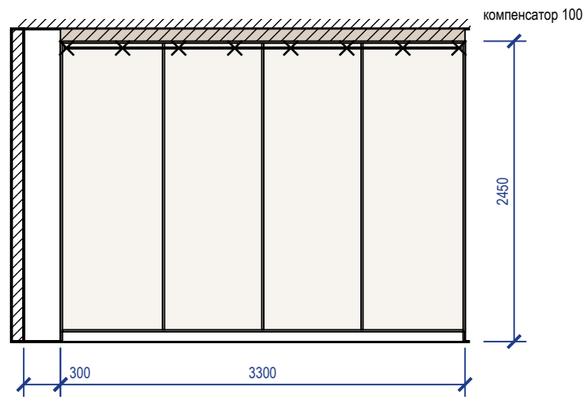


Система хранения М-22 пом. 7 (М 1:50)

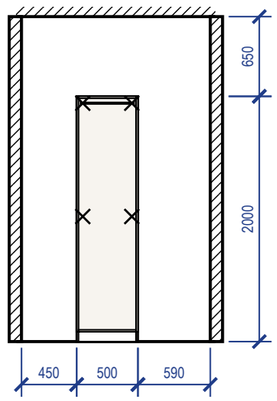

Шкаф распашной М-24 (пом. 8) (М 1:50)

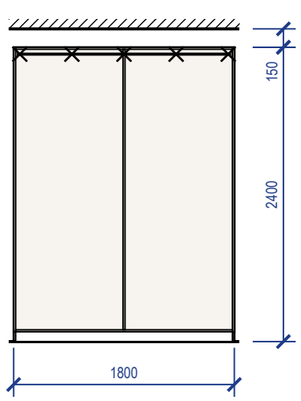

Шкаф распашной М-29 (пом. 10) (М 1:50)

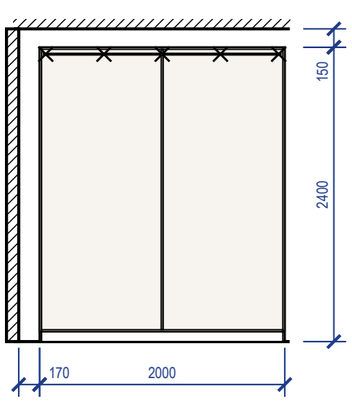

Крепление и зазоры под отделку

Марка	Помещение, стена	Основание	Отделка стены	Зазор, мм	Крепёж по планке	От опрокидывания
М-05	Кладовая (2), стена Б	по основанию — см. таблицу крепежа	окраска	5	анкер 8 шт. (2 ряда)	уголки 2 шт.
М-11	Прихожая-холл (4), стена А	по основанию — см. таблицу крепежа	окраска	5	анкер 8 шт., шаг 457	уголки 2 шт.
М-22	Постирочная (7), стена Б	по основанию — см. таблицу крепежа	окраска	5	анкер 4 шт. (2 ряда)	уголки 2 шт.
М-24	Спальня 2 (8), стена А	по основанию — см. таблицу крепежа	окраска	5	анкер 5 шт., шаг 425	уголки 2 шт.
М-29	Спальня мастер (10), стена Г	по основанию — см. таблицу крепежа	окраска	5	анкер 5 шт., шаг 475	уголки 2 шт.

Крепёж по основанию стены

Основание стены	Крепёж
бетон, ж/б	анкер-шуруп 7,5×72 или дюбель 8×60 с шурупом 5×70
кирпич полнотелый	дюбель 8×80 с шурупом 5×90
газобетон, пазогребень	дюбель для газобетона 10×100 или химический анкер
гипсокартон	закладная до обшивки (брус 40×80 или фанера 18 мм), саморез в закладную

Условные обозначения


- анкер / уголок крепления к стене
- корпус и полки ЛДСП (вид на стену)
- компенсатор — короб до потолка

Примечания

1. Установочные размеры — от чистого пола и чистых стен; перед установкой контрольный замер после отделки.
2. Порядок: корпус выставить по уровню опорами цоколя → закрепить к стене по задней планке → навесить двери и фасады, отрегулировать зазоры → подогнать и закрепить компенсатор.
3. Анкеры — с шагом не более 500 мм, не ближе 50 мм от края планки; на ГКЛ только в закладную, установленную до обшивки.
4. Скрытые коммуникации под анкеры проверить детектором; трассы электрики по плану розеток.

	Лист	№ док.	Подпись	Дата	Проект: Квартира 103 м²			М 1:50
Дизайнер	Кырлан А.С.			14.11.26	Шкафы. Монтажная схема	Стадия	Лист	Листов
Проверил						П	29	129
Н. контр.								
Утв.								

выпуск 14.11.2026 № 32d0256903 · стр. 29 из 129

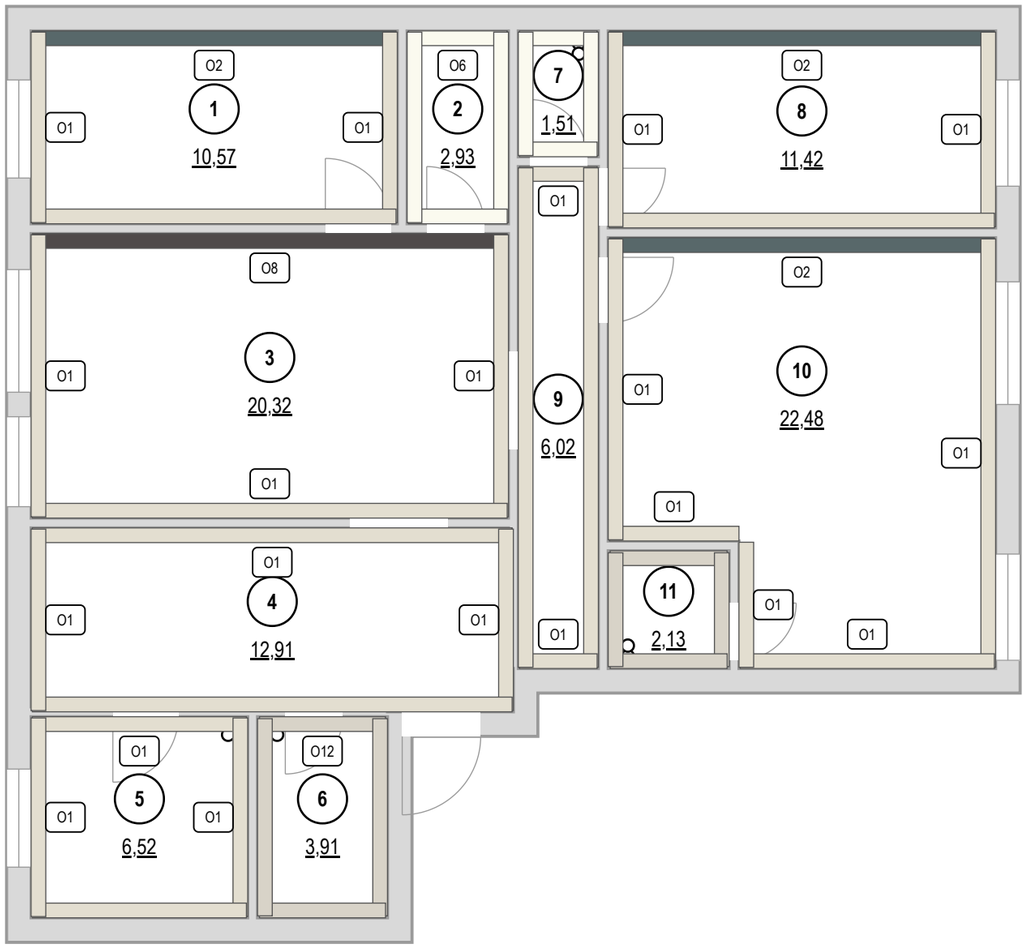

Покрытия стен

Марка	Покрытие	Помещение: S, м²	Итого, м²
O1	окраска Farrow & Ball · No. 291 «School House White — тёплый меловой белый»	1: 20,4; 3: 23,7; 4: 33,6; 5: 20,2; 8: 20,9; 9: 28,9; 10: 31,7	179,3
O2	окраска Farrow & Ball · No. 289 «Inchyra Blue — тёмный сине-серый»	1: 11,8; 8: 12,0; 10: 12,0	35,8
O6	окраска Tikkurila · S 0502-Y «Белый с лёгкой желтизной»	2: 17,3; 7: 11,6	28,9
O8	окраска Farrow & Ball · No. 255 «Tanner's Brown — тёмный шоколад»	3: 11,7	11,7
O12	облицовка плиткой Atlas Concorde · A8UZ «Marvel Travertine» 600×1200 мм	6: 17,5; 11: 12,1	29,6

Площади — нетто, по развёрткам (за вычетом проёмов и фартука); высоты помещений — от чистого пола.

	Лист	№ док.	Подпись	Дата
Дизайнер	Кырлан А.С.			14.11.26
Проверил				
Н. контр.				
Утв.				

Проект: Квартира 103 м² — **М 1:75**

Карта покрытий стен

Стадия	Лист	Листов
П	30	129

выпуск 14.11.2026 № 32d0256903 · стр. 30 из 129

Колерная карта по помещениям

Помещение	Поверхность	Образец	Поз.	Система и код цвета	Производитель, линейка / материал, артикул	Блеск	Класс истирания	LRV	Площадь
1. Кабинет-библиотека 10,57 м²	стены		**К1**	Farrow & Ball No. 291	Farrow & Ball · Modern Emulsion	матовая	1	73	19,9 м²
	акцент А		**К2**	Farrow & Ball No. 289	Farrow & Ball · Modern Emulsion	матовая	1	13	11,4 м²
	потолок		**К3**	NCS S 0502-Y	Tikkurila · Anti-Reflex 2	глубокомат.	2	95	10,6 м²
	пол		**КМ1**	по образцу	Coswick · Вековые традиции · арт. 1167-4250				10,6 м²
	плинтус		**К4**	Farrow & Ball No. 291	МДФ · в цвет Farrow & Ball			73	12,9 м
2. Кладовая 2,93 м²	стены		**К5**	NCS S 0502-Y	Tikkurila · Harmony	матовая	1	95	17,6 м²
	потолок		**К3**	NCS S 0502-Y	Tikkurila · Anti-Reflex 2	глубокомат.	2	95	2,9 м²
	пол		**КМ1**	по образцу	Coswick · Вековые традиции · арт. 1167-4250				2,9 м²
	плинтус		**К6**	NCS S 0502-Y	МДФ · в цвет NCS			95	6,5 м
3. Гостиная-столовая 20,32 м²	стены		**К1**	Farrow & Ball No. 291	Farrow & Ball · Modern Emulsion	матовая	1	73	23,6 м²
	акцент А		**К7**	Farrow & Ball No. 255	Farrow & Ball · Modern Emulsion	матовая	1	7	11,7 м²
	потолок		**К1**	Farrow & Ball No. 291	Farrow & Ball · Modern Emulsion	матовая	1	73	20,3 м²
	пол		**КМ1**	по образцу	Coswick · Вековые традиции · арт. 1167-4250				20,3 м²
	плинтус		**К8**	Farrow & Ball No. 291	МДФ · в цвет Farrow & Ball	полуглянц.	2	73	14,7 м
4. Прихожая-холл 12,91 м²	стены		**К1**	Farrow & Ball No. 291	Farrow & Ball · Modern Emulsion	матовая	1	73	33,9 м²
	потолок		**К3**	NCS S 0502-Y	Tikkurila · Anti-Reflex 2	глубокомат.	2	95	12,9 м²
	пол		**КМ2**	Marvel Travertine	Atlas Concorde · арт. A8UZ				12,9 м²
	плинтус		**К4**	Farrow & Ball No. 291	МДФ · в цвет Farrow & Ball			73	12,6 м
5. Кухня 6,52 м²	стены		**К1**	Farrow & Ball No. 291	Farrow & Ball · Modern Emulsion	матовая	1	73	20,5 м²
	потолок		**К1**	Farrow & Ball No. 291	Farrow & Ball · Modern Emulsion	матовая	1	73	6,5 м²
	пол		**КМ1**	по образцу	Coswick · Вековые традиции · арт. 1167-4250				6,5 м²
	плинтус		**К8**	Farrow & Ball No. 291	МДФ · в цвет Farrow & Ball	полуглянц.	2	73	9,4 м
	фартук		**КМ3**	тон Paper F497 (тёплый белый)	керамогранит · аналог по хар.				2,0 м²

Схема квартиры: цвет стен и акценты (б/м)

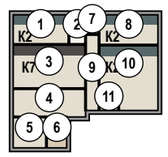


Схема палитры проекта

Стиль: Мид-сенчури 65% + Ар-деко 35% · схема: комплементарная

основной	основной	второстепенный	второстепенный	второстепенный	акцентный	акцентный	акцентный	акцентный
Farrow & Ball No. 291	NCS S 0502-Y	Farrow & Ball No. 298	Farrow & Ball No. 289	Farrow & Ball No. 255	NCS S 2050-Y20R	NCS S 3050-Y70R	NCS S 5030-B10G	NCS S 5040-B90G
School House White — тёплый меловой белый LRV 73 стены 1,3,4,5,8,9,10; плинтус 1,3,4,5,8,9,10; потолок 3,5; текстиль/декор 3	Белый с лёгкой желтизной LRV 95 потолок 1,2,4,6,7,8,9,10,11; стены 2,7; плинтус 2,7; текстиль/декор 1,8,10	Bancha — оливковый середины века LRV 14 текстиль/декор 3,10	Inchyra Blue — тёмный сине-серый LRV 13 акцент 1,8,10; текстиль/декор 1,8,10	Tanner's Brown — тёмный шоколад LRV 7 акцент 3; текстиль/декор 3	Горчичный LRV 42 текстиль/декор 1,8	Терракотовый / жжёный оранжевый LRV 18 текстиль/декор 1,8	Тил LRV 12 текстиль/декор 8	Изумрудный LRV 8 в отделке не применён

План 60/30/10



Окраска, факт — по площади стен, акцентов, потолков



окрашено всего 357 м²; второстепенный тон несут мебель и текстиль

Текстиль и декор в цветах вне палитры проекта

NCS S 1005-Y20R Светлый кремовый — пом. 1 (Т7), 3 (Т1, Т4), 5 (Т14), 8 (Т11), 10 (Т19, Т22)

Условные обозначения

- **К1** Farrow & Ball No. 291 · School House White — тёплый меловой белый · Modern Emulsion · матовая · кл. 1
- **К2** Farrow & Ball No. 289 · Inchyra Blue — тёмный сине-серый · Modern Emulsion · матовая · кл. 1
- **К3** NCS S 0502-Y · Белый с лёгкой желтизной · Tikkurila Anti-Reflex 2 · глубокомат. · кл. 2
- **К4** Farrow & Ball No. 291 · School House White — тёплый меловой белый · МДФ
- **К5** NCS S 0502-Y · Белый с лёгкой желтизной · Tikkurila Harmony · матовая · кл. 1
- **К6** NCS S 0502-Y · Белый с лёгкой желтизной · МДФ
- **К7** Farrow & Ball No. 255 · Tanner's Brown — тёмный шоколад · Modern Emulsion · матовая · кл. 1
- дерево (доска, паркет, ламинат) — рисунок досок
- керамогранит, плитка, камень — сетка швов по формату
- **К8** Farrow & Ball No. 291 · School House White — тёплый меловой белый · МДФ · полуглянц. · кл. 2
- **К9** NCS S 0502-Y · Белый с лёгкой желтизной · Tikkurila Luja 7 · матовая · кл. 1
- **КМ1** инженерная доска · 1167-4250
- **КМ2** керамогранит · A8UZ
- **КМ3** аналог: керамогранит матовый, тон F497, 600×600×9 мм
- **КМ4** плитка · A8UZ
- **КМ5** керамогранит · Atlas Concorde Marvel Travertine Sand — Cross 60×60 Matte Sensitech, арт. AFUL (той же коллекции, что стены A8UZ; тон сверить по образцу)

К — краска, КМ — отделочный материал (тон КМ — по описанию, эталон — образец материала); кл. — класс истирания (1 — самый стойкий к мытью); LRV — светлота цвета: 0 — чёрный, 100 — белый

Примечания

1. Цвет на листе и на экране — ориентир. До покраски — выкрас на объекте: не меньше А3 (или лист ГКЛ), на грунте под эту краску, не на белой шпаклёвке, в 2 слоя; на обороте — код, бренд, веер, дата. Смотреть днём и вечером, рядом с образцами пола и плитки. Красить только в цвет утверждённого выкраса.
2. Краску заказывать по коду из графы «Система и код цвета» у бренда этого кода, не «аналогом» другого; весь объём одного кода — одной партией, колеруемую краску — за один проход машины.
3. Площади — те же, что в ведомости отделки (лист С1); сколько краски заказать — в спецификации отделочных материалов (лист С3).
4. Колерная карта на 2 листах: обозначения — на каждом, схема и палитра — на первом, выкрасы — на последнем.

	Лист	№ док.	Подпись	Дата	Проект: Квартира 103 м²			
Дизайнер	Кырлан А.С.			14.11.26				
Проверил					Колерная карта	Стадия	Лист	Листов
Н. контр.						П	31	129
Утв.								

выпуск 14.11.2026 № 32d0256903 · стр. 31 из 129

Колерная карта по помещениям (продолжение)

Помещение	Поверхность	Образец	Поз.	Система и код цвета	Производитель, линейка / материал, артикул	Блеск	Класс истирания	LRV	Площадь
6. Ванная 3,91 м²	стены		**КМ4**	Marvel Travertine	Atlas Concorde · арт. A8UZ				18,0 м²
	потолок		**К9**	NCS S 0502-Y	Tikkurila · Luja 7	матовая	1	95	3,9 м²
	пол		**КМ5**	по образцу	керамогранит · Atlas Concorde Marvel Travertine Sand Cross 60×60 Matte Sensitech, арт. AFUL (той же коллекции, что стены A8UZ; тон сверить по образцу)				3,9 м²
7. Постирочная 1,51 м²	стены		**К5**	NCS S 0502-Y	Tikkurila · Harmony	матовая	1	95	11,9 м²
	потолок		**К3**	NCS S 0502-Y	Tikkurila · Anti-Reflex 2	глубокомат.	2	95	1,5 м²
	пол		**КМ1**	по образцу	Coswick · Вековые традиции · арт. 1167-4250				1,5 м²
	плинтус		**К6**	NCS S 0502-Y	МДФ · в цвет NCS			95	4,3 м
8. Спальня 2 11,42 м²	стены		**К1**	Farrow & Ball No. 291	Farrow & Ball · Modern Emulsion	матовая	1	73	20,9 м²
	акцент А		**К2**	Farrow & Ball No. 289	Farrow & Ball · Modern Emulsion	матовая	1	13	12,1 м²
	потолок		**К3**	NCS S 0502-Y	Tikkurila · Anti-Reflex 2	глубокомат.	2	95	11,4 м²
	пол		**КМ1**	по образцу	Coswick · Вековые традиции · арт. 1167-4250				11,4 м²
	плинтус		**К4**	Farrow & Ball No. 291	МДФ · в цвет Farrow & Ball			73	13,6 м
9. Коридор 6,02 м²	стены		**К1**	Farrow & Ball No. 291	Farrow & Ball · Modern Emulsion	матовая	1	73	29,2 м²
	потолок		**К3**	NCS S 0502-Y	Tikkurila · Anti-Reflex 2	глубокомат.	2	95	6,0 м²
	пол		**КМ1**	по образцу	Coswick · Вековые традиции · арт. 1167-4250				6,0 м²
	плинтус		**К4**	Farrow & Ball No. 291	МДФ · в цвет Farrow & Ball			73	10,8 м
10. Спальня мастер 22,48 м²	стены		**К1**	Farrow & Ball No. 291	Farrow & Ball · Modern Emulsion	матовая	1	73	31,5 м²
	акцент А		**К2**	Farrow & Ball No. 289	Farrow & Ball · Modern Emulsion	матовая	1	13	12,1 м²
	потолок		**К3**	NCS S 0502-Y	Tikkurila · Anti-Reflex 2	глубокомат.	2	95	22,5 м²
	пол		**КМ1**	по образцу	Coswick · Вековые традиции · арт. 1167-4250				22,5 м²
	плинтус		**К4**	Farrow & Ball No. 291	МДФ · в цвет Farrow & Ball			73	18,5 м
11. Ванная мастер 2,13 м²	стены		**КМ4**	Marvel Travertine	Atlas Concorde · арт. A8UZ				12,6 м²
	потолок		**К9**	NCS S 0502-Y	Tikkurila · Luja 7	матовая	1	95	2,1 м²
	пол		**КМ5**	по образцу	керамогранит · Atlas Concorde Marvel Travertine Sand Cross 60×60 Matte Sensitech, арт. AFUL (той же коллекции, что стены A8UZ; тон сверить по образцу)				2,1 м²

Перечень выкрасов на согласование

№	Код	Бренд / веер	Пом. / стена	Подложка	Формат	Статус
1	No. 291	Farrow & Ball	1, 3, 4, 5, 8, 9, 10	ГКЛ с грунтом; МДФ под эмаль	600×1000; 300×600	к выполнению
2	No. 289	Farrow & Ball	1 А, 8 А, 10 А	ГКЛ с грунтом	600×1000	к выполнению
3	S 0502-Y	NCS Tikkurila	1, 2, 4, 6, 7, 8, 9, 10, 11	ГКЛ с грунтом; МДФ под эмаль	600×1000; 300×600	к выполнению
4	No. 255	Farrow & Ball	3 А	ГКЛ с грунтом	600×1000	к выполнению

Примечания


1. Цвет на листе и на экране — ориентир. До покраски — выкрас на объекте: не меньше А3 (или лист ГКЛ), на грунте под эту краску, не на белой шпаклёвке, в 2 слоя; на обороте — код, бренд, веер, дата. Смотреть днём и вечером, рядом с образцами пола и плитки; к основному цвету стен — ещё 2 соседних оттенка. Красить только в цвет утверждённого выкраса.
2. Краску заказывать по коду из графы «Система и код цвета» у бренда этого кода, не «аналогом» другого; весь объём одного кода — одной партией, колеруемую краску — за один проход машины.
3. Площади — те же, что в ведомости отделки (лист С1); сколько краски заказать — в спецификации отделочных материалов (лист С3).
4. Колерная карта на 2 листах: обозначения — на каждом, схема и палитра — на первом, выкрасы — на последнем.

Условные обозначения

- **К1** Farrow & Ball No. 291 · School House White — тёплый меловой белый · Modern Emulsion · матовая · кл. 1
- **К2** Farrow & Ball No. 289 · Inchyra Blue — тёмный сине-серый · Modern Emulsion · матовая · кл. 1
- **К3** NCS S 0502-Y · Белый с лёгкой желтизной · Tikkurila Anti-Reflex 2 · глубокомат. · кл. 2
- **К4** Farrow & Ball No. 291 · School House White — тёплый меловой белый · МДФ
- **К5** NCS S 0502-Y · Белый с лёгкой желтизной · Tikkurila Harmony · матовая · кл. 1
- **К6** NCS S 0502-Y · Белый с лёгкой желтизной · МДФ
- **К7** Farrow & Ball No. 255 · Tanner's Brown — тёмный шоколад · Modern Emulsion · матовая · кл. 1
- дерево (доска, паркет, ламинат) — рисунок досок
- керамогранит, плитка, камень — сетка швов по формату
- **К8** Farrow & Ball No. 291 · School House White — тёплый меловой белый · МДФ · полуглянц. · кл. 2
- **К9** NCS S 0502-Y · Белый с лёгкой желтизной · Tikkurila Luja 7 · матовая · кл. 1
- **КМ1** инженерная доска · 1167-4250
- **КМ2** керамогранит · A8UZ
- **КМ3** аналог: керамогранит матовый, тон F497, 600×600×9 мм
- **КМ4** плитка · A8UZ
- **КМ5** керамогранит · Atlas Concorde Marvel Travertine Sand Cross 60×60 Matte Sensitech, арт. AFUL (той же коллекции, что стены A8UZ; тон сверить по образцу)

К — краска, КМ — отделочный материал (тон КМ — по описанию, эталон — образец материала); кл. — класс истирания (1 — самый стойкий к мытью); LRV — светлота цвета: 0 — чёрный, 100 — белый

	Лист	№ док.	Подпись	Дата	Проект: Квартира 103 м²			
Дизайнер	Кырлан А.С.			14.11.26				
Проверил					Колерная карта	Стадия	Лист	Листов
Н. контр.						П	32	129
Утв.								

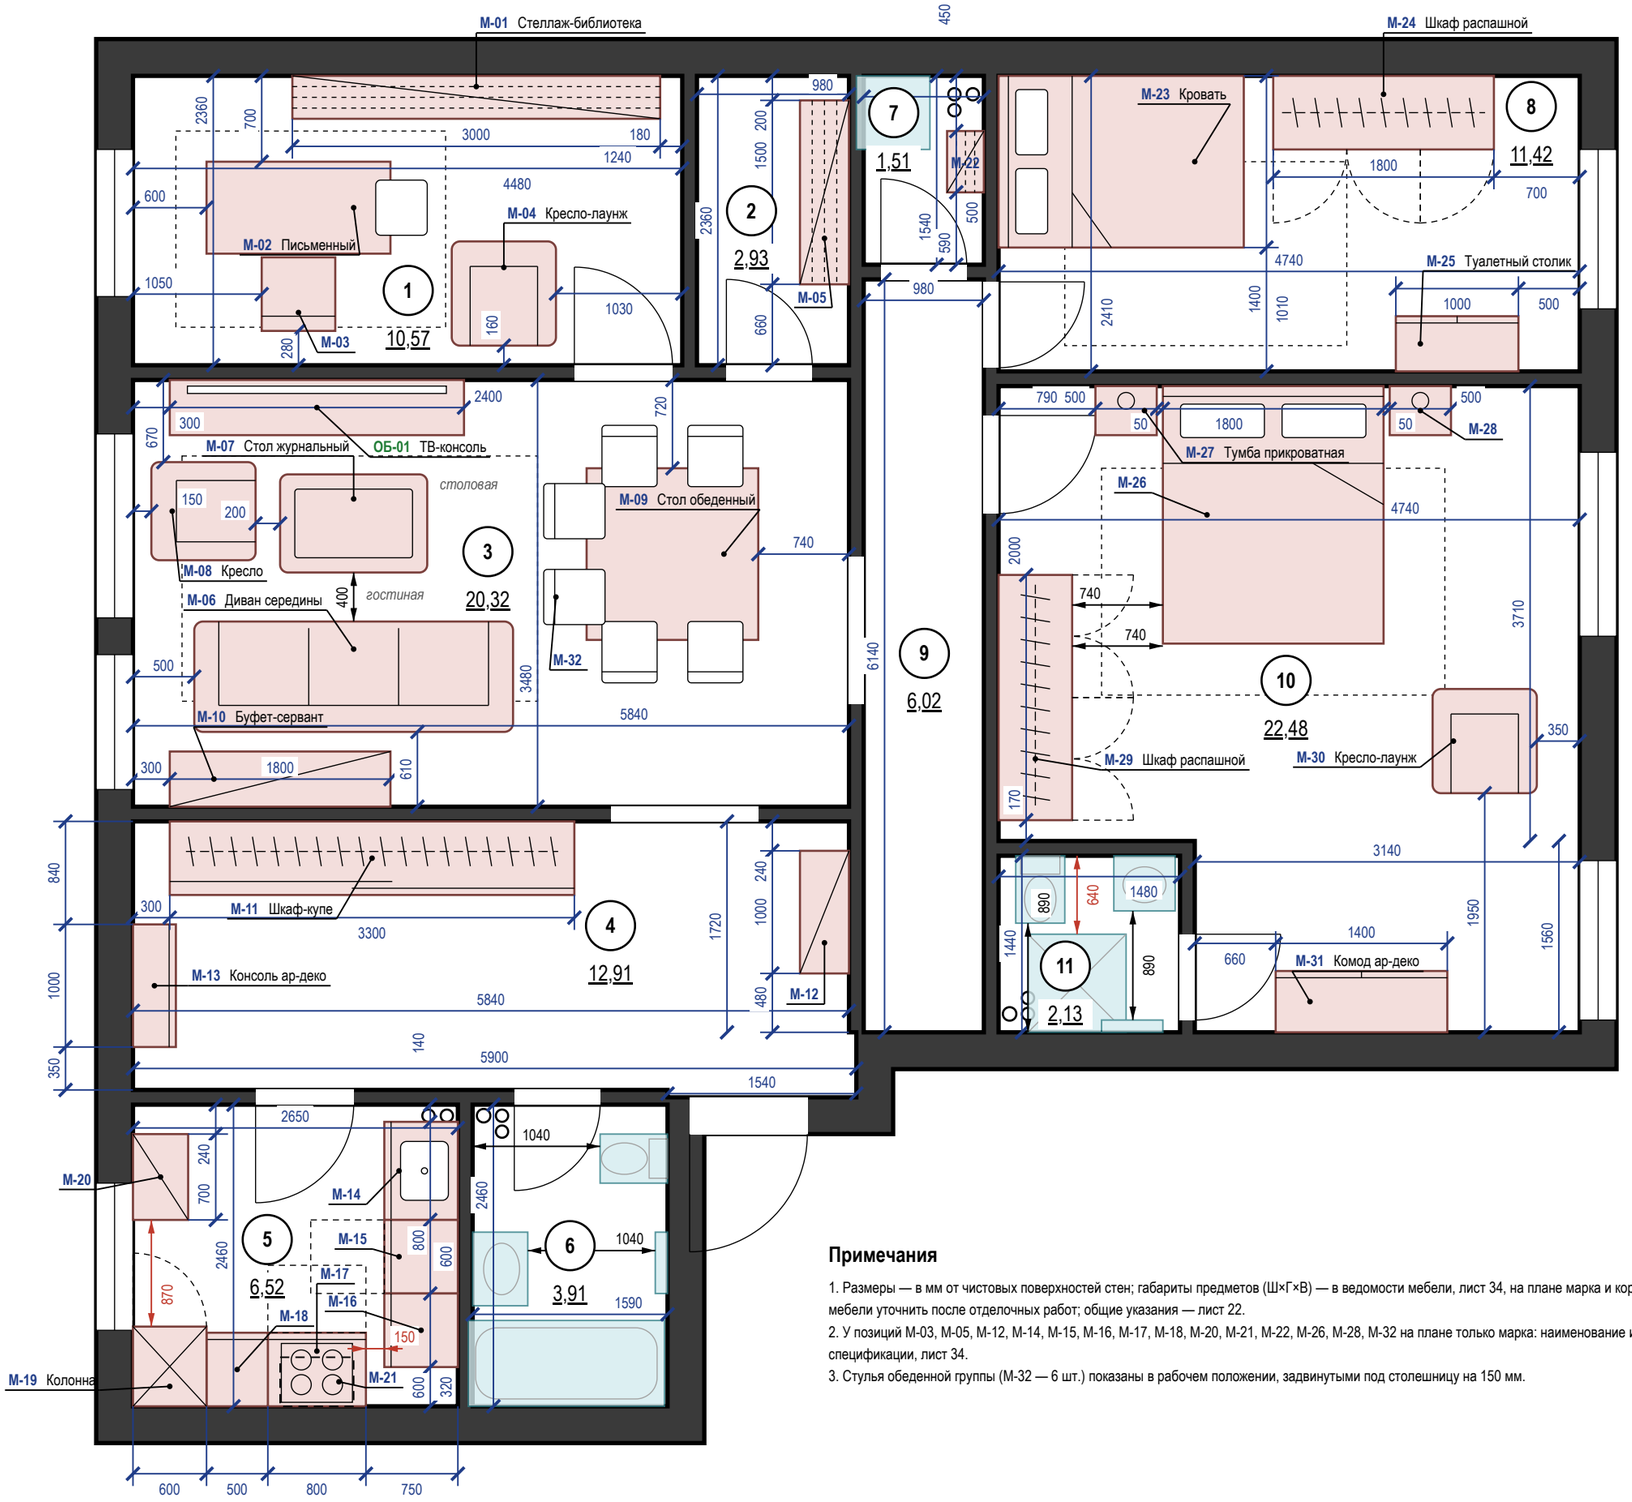

Примечания

1. Размеры — в мм от чистовых поверхностей стен; габариты предметов (Ш×Г×В) — в ведомости мебели, лист 34, на плане марка и короткое имя; размеры мебели уточнить после отделочных работ; общие указания — лист 22.
2. У позиций М-03, М-05, М-12, М-14, М-15, М-16, М-17, М-18, М-20, М-21, М-22, М-26, М-28, М-32 на плане только марка: наименование и габарит — в спецификации, лист 34.
3. Стулья обеденной группы (М-32 — 6 шт.) показаны в рабочем положении, задвинутыми под столешницу на 150 мм.

Экспликация помещений

лист 25 · на плане — номера в марках

Ведомость мебели и оборудования

Марка	Наименование	Ш×Г×В, мм	Пом.	Кол.
М-01	Стеллаж-библиотека из ореха	3000×350×2400	1	1
М-02	Письменный стол-бюро середины века	750×1500×750	1	1
М-03	Стул рабочий с подлокотниками	600×600×800	1	1
М-04	Кресло-лаунж с оттоманкой	850×850×850	1	1
М-05	Стеллаж для хранения	1500×400×2400	2	1
ОБ-01	ТВ-консоль из ореха	2400×450×550	3	1
М-06	Диван середины века	2600×900×780	3	1
М-07	Стол журнальный	1200×800×400	3	1
М-08	Кресло	800×850×1070	3	1
М-09	Стол обеденный на одной ножке	1400×1400×730	3	1
М-10	Буфет-сервант из ореха	1800×450×750	3	1
М-11	Шкаф-купе	3300×600×2450	4	1
М-12	Банкетка	1000×400×450	4	1
М-13	Консоль ар-деко	1000×350×800	4	1
М-14	Модуль под мойку	800×600×900	5	1
М-15	Посудомоечная машина встроенная	600×600×900	5	1
М-16	Модуль с ящиками	600×600×900	5	1
М-17	Модуль с варочной панелью	800×600×900	5	1
М-18	Модуль с ящиками между	500×600×900	5	1
М-19	Колонна с холодильником	600×650×2100	5	1
М-20	Стол барный у окна	700×450×900	5	1
М-21	Вытяжка над варочной панелью	600×400×600	5	1
М-22	Полки для хранения	500×300×2000	7	1
М-23	Кровать 1400×2000	1400×2000×450	8	1
М-24	Шкаф распашной	1800×600×2400	8	1
М-25	Туалетный столик середины века	1000×450×750	8	1
М-26	Кровать 1800×2100	1800×2100×450	10	1
М-27	Тумба прикроватная	500×400×550	10	1
М-28	Тумба прикроватная	500×400×550	10	1
М-29	Шкаф распашной	2000×600×2400	10	1
М-30	Кресло-лаунж с оттоманкой	850×850×850	10	1
М-31	Комод ар-деко	1400×500×800	10	1
М-32	Стул обеденный к столу М-09	450×500×820	3	6

Ш — вдоль стены (изголовья), Г — от стены (длина кровати)

Материалы, модели, допуск замены — лист 34

	Лист	№ док.	Подпись	Дата			
Дизайнер	Кырлан А.С.			14.11.26	Проект: Квартира 103 м²		М 1:50
Проверил					План размещения мебели и оборудования	Стадия	Лист	Листов
Н. контр.						П	33	129
Утв.								

выпуск 14.11.2026 № 32d0256903 · стр. 33 из 129

Поз.	Наименование и техническая характеристика	Тип, марка, обозначение документа, опросного листа	Код продукции	Поставщик	Ед. измерения	Кол.	Масса 1 ед., кг	Примечание
	Мебель встроенная и корпусная (изготовление по чертежам мебельщика)							
М-05	Стеллаж для хранения; каркас и полки — ЛДСП декор «орех» 16 мм; без фасадов; Ш×Г×В 1500×400×2400 мм	—	—	изготовление на заказ	шт.	1	—	пом. 2
М-11	Шкаф-купе; корпус ЛДСП 16 мм; фасады — МДФ, шпон ореха 10 мм, масло матовое в профиле: латунь; Ш×Г×В 3300×600×2450 мм	—	—	изготовление на заказ	шт.	1	—	пом. 4
М-14	Модуль под мойку; корпус ЛДСП 16 мм; фасады — МДФ, шпон ореха 18 мм, масло матовое; Ш×Г×В 800×600×900 мм	—	—	изготовление на заказ	шт.	1	—	пом. 5
М-15	Модуль под встраиваемую ПММ 60; без корпуса (ниша между соседними модулями); фасад на дверь машины — МДФ 18 мм, эмаль матовая; цоколь; цвет фасадов — в цвет стен (Farrow & Ball No. 291); Ш×Г×В 600×600×900 мм	—	—	изготовление на заказ	шт.	1	—	пом. 5
М-16	Модуль с ящиками; корпус ЛДСП 16 мм; фасады — МДФ 18 мм, эмаль матовая; цвет фасадов — в цвет стен (Farrow & Ball No. 291); Ш×Г×В 600×600×900 мм	—	—	изготовление на заказ	шт.	1	—	пом. 5
М-17	Модуль с варочной панелью (индукция) и духовым шкафом; корпус ЛДСП 16 мм; фасады — МДФ 18 мм, эмаль матовая; цвет фасадов — в цвет стен (Farrow & Ball No. 291); Ш×Г×В 800×600×900 мм	—	—	изготовление на заказ	шт.	1	—	пом. 5
М-18	Модуль с ящиками между колонной и плитой; корпус ЛДСП 16 мм; фасады — МДФ 18 мм, эмаль матовая; цвет фасадов — в цвет стен (Farrow & Ball No. 291); Ш×Г×В 500×600×900 мм	—	—	изготовление на заказ	шт.	1	—	пом. 5
М-19	Колонна с холодильником, ретро-фасад; корпус ЛДСП 16 мм; фасады — МДФ эмаль 18 мм, матовая; цвет — тил (S 5030-B10G); Ш×Г×В 600×650×2100 мм	—	—	изготовление на заказ	шт.	1	—	пом. 5
М-21	Вытяжка над варочной панелью; корпус ЛДСП 16 мм; фасады — МДФ 18 мм, эмаль матовая; цвет фасадов — в цвет стен (Farrow & Ball No. 291); Ш×Г×В 600×400×600 мм	—	—	изготовление на заказ	шт.	1	—	пом. 5
М-22	Полки для хранения (стена Б, в стороне от короба стояков); каркас и полки — ЛДСП 16 мм, декор «дуб натуральный»; без фасадов; Ш×Г×В 500×300×2000 мм	—	—	изготовление на заказ	шт.	1	—	пом. 7
М-24	Шкаф распашной, латунные ручки; корпус ЛДСП 16 мм; фасады — МДФ, шпон ореха 18 мм, масло матовое; Ш×Г×В 1800×600×2400 мм	—	—	изготовление на заказ	шт.	1	—	пом. 8
М-29	Шкаф распашной; корпус ЛДСП 16 мм; фасады — МДФ, шпон ореха 18 мм, масло матовое; вставка — латунь; Ш×Г×В 2000×600×2400 мм	—	—	изготовление на заказ	шт.	1	—	пом. 10
	Мебель покупная							
М-01	Стеллаж-библиотека из ореха на всю стену, латунные полкодержатели; шпон, дуб натуральный, матовое масло; Ш×Г×В 3000×350×2400 мм	аналог: Ш×Г×В 3000×350×2400 мм, шпон	—	аналог по характеристикам	шт.	1	—	пом. 1; замена ≤ габарита
М-02	Письменный стол-бюро середины века, орех, конические ножки; шпон, дуб натуральный, матовое масло; Ш×Г×В 750×1500×750 мм	аналог: Ш×Г×В 750×1500×750 мм, шпон	—	аналог по характеристикам	шт.	1	—	пом. 1; замена ≤ габарита
М-03	Стул рабочий с подлокотниками, гнутая фанера и кожа; обивка — ткань, цвет Farrow & Ball No. 298; каркас — дуб натуральный; Ш×Г×В 600×600×800 мм	аналог: Ш×Г×В 600×600×800 мм, обивка — ткань	—	аналог по характеристикам	шт.	1	—	пом. 1; замена ≤ габарита
М-04	Кресло-лаунж с оттоманкой (в духе Eames Lounge Chair), палисандровый шпон, чёрная кожа; обивка — ткань, цвет Farrow & Ball No. 298; Ш×Г×В 850×850×850 мм	аналог: Ш×Г×В 850×850×850 мм, обивка — ткань	—	аналог по характеристикам	шт.	1	—	пом. 1; замена ≤ габарита
М-06	Диван середины века (в духе Florence Knoll), букле горчичного цвета, латунные опоры; обивка — ткань, цвет Farrow & Ball No. 298; Ш×Г×В 2600×900×780 мм	аналог: Ш×Г×В 2600×900×780 мм, обивка — ткань	—	аналог по характеристикам	шт.	1	—	пом. 3; замена ≤ габарита
М-07	Стол журнальный (в духе Noguchi Coffee Table), орех и стекло; шпон, дуб натуральный, матовое масло; Ш×Г×В 1200×800×400 мм	аналог: Ш×Г×В 1200×800×400 мм, шпон	—	аналог по характеристикам	шт.	1	—	пом. 3; замена ≤ габарита
М-08	Кресло (в духе Egg Chair), изумрудный бархат; обивка — ткань, цвет Farrow & Ball No. 298; Ш×Г×В 800×850×1070 мм	аналог: Ш×Г×В 800×850×1070 мм, обивка — ткань	—	аналог по характеристикам	шт.	1	—	пом. 3; замена ≤ габарита
М-09	Стол обеденный на одной ножке (в духе Tulip Table), мрамор Calacatta, d 1400; шпон, дуб натуральный, матовое масло; Ш×Г×В 1400×1400×730 мм	аналог: Ш×Г×В 1400×1400×730 мм, шпон	—	аналог по характеристикам	шт.	1	—	пом. 3; замена ≤ габарита
М-10	Буфет-сервант из ореха на конических ножках, раздвижные двери; шпон, дуб натуральный, матовое масло; Ш×Г×В 1800×450×750 мм	аналог: Ш×Г×В 1800×450×750 мм, шпон	—	аналог по характеристикам	шт.	1	—	пом. 3; замена ≤ габарита
М-32	Стул обеденный к столу М-09; обивка — ткань, цвет Farrow & Ball No. 298; каркас — дуб натуральный; Ш×Г×В 450×500×820 мм	аналог: Ш×Г×В 450×500×820 мм, обивка — ткань	—	аналог по характеристикам	шт.	6	—	пом. 3; замена ≤ габарита
ОБ-01	ТВ-консоль из ореха на конических ножках, ТВ на стене; шпон, дуб натуральный, матовое масло; Ш×Г×В 2400×450×550 мм	аналог: Ш×Г×В 2400×450×550 мм, шпон	—	аналог по характеристикам	шт.	1	—	пом. 3; замена ≤ габарита
М-12	Банкетка, изумрудный бархат, латунные ножки; Ш×Г×В 1000×400×450 мм	аналог: Ш×Г×В 1000×400×450 мм	—	аналог по характеристикам	шт.	1	—	пом. 4; замена ≤ габарита

Примечания

1. Позиции мебели совпадают с марками на плане расстановки; размеры Ш×Г×В — Ш вдоль стены, Г от стены.
2. Размеры и привязки плана расстановки — в мм от чистовых поверхностей стен: слой штукатурки 20 мм по блоку и 5 мм шпаклёвки по ГКЛ учтён; привязки — от стен и углов помещения, а не от другой мебели.
3. План расстановки не является документацией для изготовления мебели. Встроенная и корпусная мебель изготавливается по чертежам мебельщика после контрольного обмера (после штукатурки); «стена в стену» — с зазором 10 мм с каждой стороны или с компенсаторами; графы «Тип, марка» и «Код продукции» для неё не заполняются (ГОСТ 21.110-2013).
4. Покупные изделия — аналог по характеристикам: заменять только на изделия не больше указанного габарита и того же материала и цвета.
5. Материал и цвет, не указанные в данных изделия, приняты по концепции: тон дерева — по полу, обивка — по вторичному цвету палитры; образцы согласовать до заказа.
6. Масса 1 ед. для изделий до 25 кг не указывается. Техника — по монтажным схемам изготовителя; выводы — по листам ЭОМ и ВК.

	Лист	№ док.	Подпись	Дата	Проект: Квартира 103 м²			
Дизайнер	Кырлан А.С.			14.11.26	Спецификация мебели и оборудования	Стадия	Лист	Листов
Проверил						П	34	129
Н. контр.								
Утв.								

Поз.	Наименование и техническая характеристика	Тип, марка, обозначение документа, опросного листа	Код продукции	Поставщик	Ед. измерения	Кол.	Масса 1 ед., кг	Примечание
М-13	Консоль ар-деко, чёрный лак и латунь; шпон, дуб натуральный, матовое масло; Ш×Г×В 1000×350×800 мм	аналог: Ш×Г×В 1000×350×800 мм, шпон	—	аналог по характеристикам	шт.	1	—	пом. 4; замена ≤ габарита
М-20	Стол барный у окна, терраццо; Ш×Г×В 700×450×900 мм	аналог: Ш×Г×В 700×450×900 мм	—	аналог по характеристикам	шт.	1	—	пом. 5; замена ≤ габарита
М-23	Кровать 1400×2000, изголовье с каннелюрами, бархат цвета тил; мягкое изголовье, обивка — ткань, цвет Farrow & Ball No. 298; Ш×Г×В 1400×2000×450 мм	аналог: Ш×Г×В 1400×2000×450 мм, мягкое изголовье	—	аналог по характеристикам	шт.	1	—	пом. 8; замена ≤ габарита
М-25	Туалетный столик середины века с круглым зеркалом; шпон, дуб натуральный, матовое масло; Ш×Г×В 1000×450×750 мм	аналог: Ш×Г×В 1000×450×750 мм, шпон	—	аналог по характеристикам	шт.	1	—	пом. 8; замена ≤ габарита
М-26	Кровать 1800×2100 с высоким изголовьем ар-деко, изумрудный бархат, латунный кант; мягкое изголовье, обивка ткань, цвет Farrow & Ball No. 298; Ш×Г×В 1800×2100×450 мм	аналог: Ш×Г×В 1800×2100×450 мм, мягкое изголовье	—	аналог по характеристикам	шт.	1	—	пом. 10; замена ≤ габарита
М-27, М-28	Тумба прикроватная, орех и латунь; шпон, дуб натуральный, матовое масло; Ш×Г×В 500×400×550 мм	аналог: Ш×Г×В 500×400×550 мм, шпон	—	аналог по характеристикам	шт.	2	—	пом. 10; замена ≤ габарита
М-30	Кресло-лаунж с оттоманкой (в духе Eames Lounge Chair), коньячная кожа; обивка — ткань, цвет Farrow & Ball No. 298; Ш×Г×В 850×850×850 мм	аналог: Ш×Г×В 850×850×850 мм, обивка — ткань	—	аналог по характеристикам	шт.	1	—	пом. 10; замена ≤ габарита
М-31	Комод ар-деко, макассар и латунь; шпон, дуб натуральный, матовое масло; Ш×Г×В 1400×500×800 мм	аналог: Ш×Г×В 1400×500×800 мм, шпон	—	аналог по характеристикам	шт.	1	—	пом. 10; замена ≤ габарита
	Техника встраиваемая и бытовая (покупные изделия), светильники под розетки							
	Посудомоечная машина встраиваемая, в модуле М-15; ниша 600 мм	аналог по характеристикам: полновстраиваемая 60 см под фасад, ниша 600 × 862 мм, навеска фасада в комплекте	—	по выбору заказчика до изготовления мебели	шт.	1	—	пом. 5; по схеме изготовителя
	Духовой шкаф встраиваемый, в модуле М-17	аналог по характеристикам: 60 см, лицевая панель 595 мм, ниша 560 × 600, глубина ≥ 550 мм, вентиляция за прибором	—	по выбору заказчика до изготовления мебели	шт.	1	—	пом. 5; по схеме изготовителя
	Холодильник встраиваемый, в модуле М-19	аналог по характеристикам: полновстраиваемый под фасад, ниша 1780 × 560 × 550 мм, вентиляция решётка в цоколе, выход сверху	—	по выбору заказчика до изготовления мебели	шт.	1	—	пом. 5; по схеме изготовителя
	Вытяжка, в модуле М-21	аналог по характеристикам: производительность — по расчёту ОВ, шум ≤ 55 дБ(А)	—	по выбору заказчика до изготовления мебели	шт.	1	—	пом. 5; по схеме изготовителя
	Варочная панель встраиваемая, индукционная, в модуле М-17	аналог по характеристикам: индукционная 60 см, вырез 560 × 490 мм по шаблону модели	—	по выбору заказчика до изготовления мебели	шт.	1	—	пом. 5; по схеме изготовителя
	Стиральная машина, место по листу ВК (ОБ-02); Ш×Г 600×600 мм	аналог по характеристикам: тип загрузки — по листу ВК, в плане 600 × 600 мм (ширина × глубина), по листу ВК	—	по выбору заказчика до изготовления мебели	шт.	1	—	пом. 7; по схеме изготовителя
	Торшер, у поз. М-10; абажур — ткань или опаловое стекло; лампа 2700 K	—	—	аналог по характеристикам	шт.	1	—	пом. 3; розетка Р3 (ЭОМ)
	Текстиль							
Т7	Портьеры-волна; лён 100 %; цвет NCS S 1005-Y20R; карниз 1820 мм, высота 2640 мм, сборка 2	—	—	аналог по характеристикам	шт.	2	—	пом. 1
Т8	Тюль; полиэстер 100 %; цвет NCS S 0502-Y; карниз 1820 мм, высота 2640 мм, сборка 2,5	—	—	аналог по характеристикам	шт.	1	—	пом. 1
Т9	Ковёр под рабочей зоной, геометрия середины века; шерсть 100 %; цвет NCS S 2050-Y20R; 2200×1600 мм	—	—	аналог по характеристикам	шт.	1	—	пом. 1; с подложкой
Т10	Подушки декоративные на кровать; букле (шерсть 60 %, полиэстер 40 %); цвет NCS S 3050-Y70R	—	—	аналог по характеристикам	шт.	3	—	пом. 1
Т12	Плед на кровать; шерсть мериноса 100 %; цвет Farrow & Ball No. 289	—	—	аналог по характеристикам	шт.	1	—	пом. 1
Т1	Портьеры-волна, два полотна; лён 100 %; цвет NCS S 1005-Y20R; карниз 2150 мм, высота 2640 мм, сборка 2	—	—	аналог по характеристикам	шт.	2	—	пом. 3
Т2	Тюль-вуаль, одно полотно; полиэстер 100 %; цвет Farrow & Ball No. 291; карниз 2150 мм, высота 2640 мм, сборка 2,5	—	—	аналог по характеристикам	шт.	1	—	пом. 3
Т3	Ковёр мягкой группы, абстрактная геометрия середины века; шерсть 100 %; цвет Farrow & Ball No. 298; 2900×2000 мм	—	—	аналог по характеристикам	шт.	1	—	пом. 3; с подложкой

	Лист	№ док.	Подпись	Дата
Дизайнер	Кырлан А.С.			14.11.26
Проверил				
Н. контр.				
Утв.				

Проект: Квартира 103 м²

Спецификация мебели и оборудования (продолжение)	Стадия	Лист	Листов
	П	35	129

Поз.	Наименование и техническая характеристика	Тип, марка, обозначение документа, опросного листа	Код продукции	Поставщик	Ед. измерения	Кол.	Масса 1 ед., кг	Примечание
Т4	Подушки декоративные на диван; лён 100 %; цвет NCS S 1005-Y20R	—	—	аналог по характеристикам	шт.	3	—	пом. 3
Т5	Подушки декоративные на диван, акцент; хлопковый бархат 100 %; цвет Farrow & Ball No. 255	—	—	аналог по характеристикам	шт.	2	—	пом. 3
Т6	Плед на диван; шерсть мериноса 100 %; цвет Farrow & Ball No. 255	—	—	аналог по характеристикам	шт.	1	—	пом. 3
Т14	Рулонная штора кассетная, ткань димаут; полиэстер 100 %; цвет NCS S 1005-Y20R; карниз 1600 мм, высота 1750 мм	—	—	аналог по характеристикам	шт.	1	—	пом. 5
Т11	Портьеры-волна; лён 100 %; цвет NCS S 1005-Y20R; карниз 1820 мм, высота 2640 мм, сборка 2	—	—	аналог по характеристикам	шт.	2	—	пом. 8
Т13	Тюль; полиэстер 100 %; цвет NCS S 0502-Y; карниз 1820 мм, высота 2640 мм, сборка 2,5	—	—	аналог по характеристикам	шт.	1	—	пом. 8
Т15	Ковёр под кроватью; шерсть 100 %; цвет NCS S 2050-Y20R; 2300×1500 мм	—	—	аналог по характеристикам	шт.	1	—	пом. 8; с подложкой
Т16	Подушки декоративные на кровать; букле (шерсть 60 %, полиэстер 40 %); цвет NCS S 3050-Y70R	—	—	аналог по характеристикам	шт.	3	—	пом. 8
Т17	Подушки на кровать, акцент; хлопковый бархат 100 %; цвет NCS S 5030-B10G	—	—	аналог по характеристикам	шт.	2	—	пом. 8
Т18	Плед на кровать; шерсть мериноса 100 %; цвет Farrow & Ball No. 289	—	—	аналог по характеристикам	шт.	1	—	пом. 8
Т19	Портьеры-волна; лён 100 %; цвет NCS S 1005-Y20R; карниз 2500 мм, высота 2640 мм, сборка 2	—	—	аналог по характеристикам	шт.	2	—	пом. 10
Т20	Тюль; полиэстер 100 %; цвет NCS S 0502-Y; карниз 2500 мм, высота 2640 мм, сборка 2,5	—	—	аналог по характеристикам	шт.	1	—	пом. 10
Т21	Ковёр под кроватью; шерсть 80 %, хлопок 20 %; цвет Farrow & Ball No. 298; 2800×1850 мм	—	—	аналог по характеристикам	шт.	1	—	пом. 10; с подложкой
Т22	Подушки декоративные на кровать; лён 100 %; цвет NCS S 1005-Y20R	—	—	аналог по характеристикам	шт.	3	—	пом. 10
Т23	Подушки на кровать, акцент; хлопковый бархат 100 %; цвет Farrow & Ball No. 289	—	—	аналог по характеристикам	шт.	2	—	пом. 10
Т24	Плед на кровать; шерсть мериноса 100 %; цвет Farrow & Ball No. 289	—	—	аналог по характеристикам	шт.	1	—	пом. 10
	Декор							
ДК3	Картина над креслом: графика середины века, рама — орех; 1000×700 мм; низ на 1100 мм от пола	—	—	аналог по характеристикам	шт.	1	4	пом. 1; крепление к стене
ДК1	Картина над буфетом: абстракция середины века, рама — латунь; 1200×900 мм; низ на 1000 мм от пола	—	—	аналог по характеристикам	шт.	1	6	пом. 3; крепление: планка на дюбелях, 4 точки
ДК2	Фикус лировидный в кашпо Ø400; 450×450 мм	—	—	аналог по характеристикам	шт.	1	—	пом. 3
ДК5	Зеркало; рама — чёрный матовый; 800×1800 мм; низ на 550 мм от пола	—	—	аналог по характеристикам	шт.	1	18	пом. 4; крепление: анкер, 4 шт.
ДК8	Часы настенные Ø400; 400×400 мм; центр на 1550 мм от пола	—	—	аналог по характеристикам	шт.	1	2	пом. 5; крепление: дюбель с крюком, 1 точка
ДК9	Хлорофитум хохлатый на подоконнике (отм. +0,800); 300×200 мм; низ на 800 мм от пола	—	—	аналог по характеристикам	шт.	1	—	пом. 5
ДК4	Картина над кроватью: графика в паспарту, рама — дуб; 1000×700 мм; низ на 1100 мм от пола	—	—	аналог по характеристикам	шт.	1	4	пом. 8; крепление к стене
ДК6	Зеркало в рост в тонкой чёрной раме; рама — чёрный матовый; 600×1600 мм; низ на 300 мм от пола	—	—	аналог по характеристикам	шт.	1	12	пом. 8; крепление: анкер для пустотелых оснований, 4 шт.
ДК7	Картина над кроватью: абстракция, холст, тонкая рама из дуба; 1200×700 мм; низ на 1300 мм от пола	—	—	аналог по характеристикам	шт.	1	4	пом. 10; крепление к стене

	Лист	№ док.	Подпись	Дата
Дизайнер	Кырлан А.С.			14.11.26
Проверил				
Н. контр.				
Утв.				

Проект: Квартира 103 м²

Спецификация мебели и оборудования (продолжение)

Стадия	Лист	Листов
П	36	129

Ведомость изделий

Марка	Наименование	Пом.	Ш×Г×В, мм	Корпус	Фасад	Кромка, мм	Кол.
М-05	Система хранения	2	1500×400×2400	ЛДСП декор «орех» 16	без фасадов	0,4 / 2 *	1
М-11	Шкаф-купе	4	3300×600×2450	ЛДСП 16	МДФ, шпон ореха 10 мм, масло матовое в профиле: латунь	0,4 / 2 *	1
М-22	Система хранения	7	500×300×2000	ЛДСП 16	без фасадов	0,4 / 2 *	1
М-24	Шкаф распашной	8	1800×600×2400	ЛДСП 16	МДФ, шпон ореха 18 мм, масло матовое	0,4 / 2 *	1
М-29	Шкаф распашной	10	2000×600×2400	ЛДСП 16	МДФ, шпон ореха 18 мм, масло матовое; вставка — латунь	0,4 / 2 *	1
М-14	Модуль нижний: мойка	5	800×600×900	ЛДСП 16	МДФ, шпон ореха 18 мм, масло матовое	0,4 / 2 *	1
М-15	Модуль под ПММ 60: без корпуса, фасад на дверь машины	5	600×600×900	без корпуса	МДФ 18 мм, эмаль матовая — на дверь машины (навеска из её комплекта), цоколь		1
М-16	Модуль нижний: ящики	5	600×600×900	ЛДСП 16	МДФ 18 мм, эмаль матовая	0,4 / 2 *	1
М-17	Модуль нижний: духовой шкаф, варочная	5	800×600×900	ЛДСП 16	МДФ 18 мм, эмаль матовая	0,4 / 2 *	1
М-21	Модуль навесной: полки	5	600×400×600	ЛДСП 16	МДФ 18 мм, эмаль матовая	0,4 / 2 *	1
М-18	Модуль нижний: ящики	5	500×600×900	ЛДСП 16	МДФ 18 мм, эмаль матовая	0,4 / 2 *	1
М-19	Пенал: холодильник встр.	5	600×650×2100	ЛДСП 16	МДФ эмаль 18 мм, матовая; цвет тил (S 5030-B10G)	0,4 / 2 *	1

Ведомость встраиваемой техники

Поз.	Прибор	Ниша, вырез, мм	Вентиляция	Питание	Схема
М-14	Мойка врезная / подстольная с сифоном	вырез по шаблону, ориентир 700 × 480		смеситель — выводы ВК	по модели
М-15	Посудомоечная машина встраиваемая, 60 см	ниша 600 × 862 (от пола до низа столешницы)	зазор в цоколе, по схеме	Р26: М-16, Н=300 — в соседнем модуле, за ящиком	по модели
М-17	Духовой шкаф встраиваемый, 60 см	ниша 560 × 600, глубина ≥ 550	зазор за шкафом, вырез в задней стенке	ЭВ2: М-17, Н=150 — под духовым шкафом, доступ через ящик	по модели
М-17	Варочная панель индукционная, 60 см	вырез в столешнице 560 × 490		ЭВ1: М-18, Н=600 — в соседнем модуле, за ящиком	по модели
М-19	Холодильник встраиваемый, ниша 1780	ниша 1780 × 560 × 550	решётка в цоколе, канал за корпусом, выход сверху	Р20: М-19, Н=2000 — над нишей холодильника, съёмная панель	по модели
М-21	Вытяжка встраиваемая в навесной модуль, 60 см	низ ≥ 650 над панелью	воздуховод к вентканалу, короб до потолка	Р21: М-21, Н=2250 — в навесном модуле	по модели

Ведомость фурнитуры


№	Фурнитура	Тип, размер	Изделия	Кол.
1	Полкодержатель с фиксацией	ø5 мм	М-05, М-11, М-22, М-24, М-29, М-21, М-19	136
2	Штанга выдвижная торцевая	L по глубине	М-05	1
3	Опора регулируемая с цоколем на клипсах	ход 20 мм	М-05, М-11, М-22, М-24, М-29	38
4	Анкер по основанию стены	по таблице крепежа	М-05, М-11, М-22, М-24, М-29, М-21	32
5	Уголок крепления к стене от опрокидывания	стальной	М-05, М-11, М-22, М-24, М-29, М-19	12
6	Система дверей купе: профиль, направляющие, ролики	на 4 двери	М-11	1
7	Ручка-профиль вертикальная	в цвет профиля	М-11	4
8	Штанга овальная 30×15, L = 817	+ 2 держателя	М-11	1
9	Полка для обуви выдвижная наклонная	ширина 817	М-11	3
10	Полка для обуви выдвижная наклонная	ширина 794	М-11	3
11	Штанга овальная 30×15, L = 794	+ 2 держателя	М-11	1
12	Петля накладная 110° с доводчиком	чашка 35 мм	М-24, М-29, М-14, М-21, М-19	63
13	Штанга овальная 30×15, L = 876	+ 2 держателя	М-24	1
14	Штанга овальная 30×15, L = 976	+ 2 держателя	М-29	1
15	Ручка-профиль	латунь матовая	М-14, М-15, М-16, М-17, М-21, М-18, М-19	15
16	Опора кухонная регулируемая 100–120 мм	+ клипса цоколя	М-14, М-16, М-17, М-18, М-19	24
17	Комплект навески фасада ПММ	из поставки машины	М-15	1
18	Направляющие полного выдвижения с доводчиком NL 500	пара	М-16, М-17, М-18	7
19	Навес регулируемый для навесного шкафа	пара на секцию	М-21	1
20	Шина монтажная	L = 540	М-21	1

Примечания


1. Модели техники выбирает заказчик до изготовления мебели; ниши, вырезы и вентиляция — по монтажной схеме выбранной модели (условие гарантии), её номер вносится в ведомость.
2. Количество фурнитуры — по чертежам изделий; запас крепежа 5 %. Аналоги — по характеристикам (доводчик, нагрузка, ход).
3. Цвет корпусов, фасадов и профилей — по колерной карте проекта. Кромка — скрытые / видимые торцы, мм.
4. Кромка в данных изделия не задана: принята ПВХ 0,4 мм на скрытых торцах и 2 мм на видимых (по умолчанию для ЛДСП корпуса и МДФ фасада); заказчик или мебельщик подтверждает до раскроя.

	Лист	№ док.	Подпись	Дата	Проект: Квартира 103 м²			
Дизайнер	Кырлан А.С.			14.11.26	Ведомости изделий, техники и фурнитуры	Стадия	Лист	Листов
Проверил						П	37	129
Н. контр.								
Утв.								


Фрагмент 1. Ванная, пом. 6 (М 1:50)

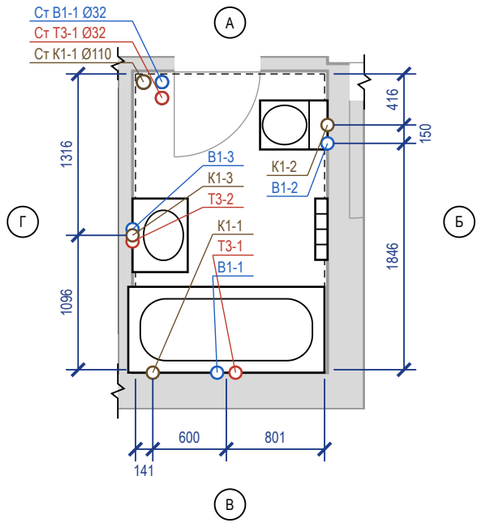


Фрагмент 2. Постирочная, пом. 7 (М 1:50)

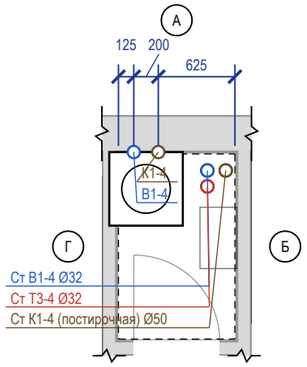

Фрагмент 3. Ванная мастер, пом. 11 (М 1:50)

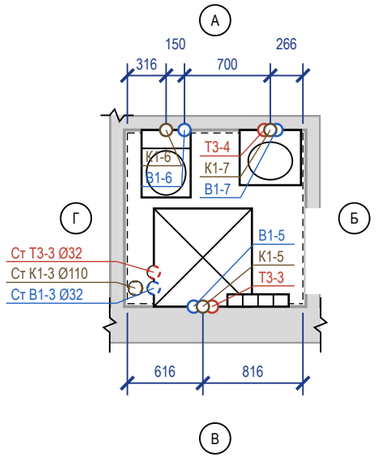

Фрагмент 4. Кухня, пом. 5 (М 1:50)

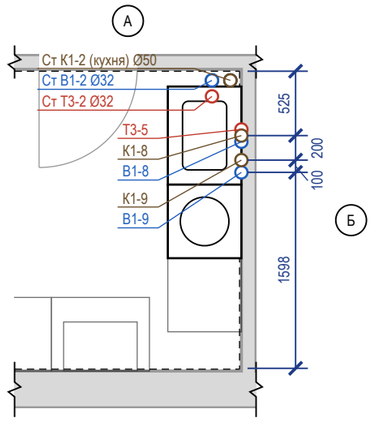

Ведомость привязок выводов

Код	Прибор	Ø	H, мм	Привязка от чист. стен, мм	Прим.
В1-1	С-01 ванна	½"	800	ст. В: 666 от Г	межос. 150
Т3-1	— "	½"	800	ст. В: 726 от Б	межос. 150
К1-1	— "	Ø50	50	ст. В: 141 от Г	
В1-2	С-02 унитаз подвесной	½"	250	ст. Б: 566 от А	в раме инсталляции
К1-2	— "	Ø110	220	ст. Б: 416 от А	
В1-3	С-03 умывальник	½"	600	ст. Г: 1146 от В	межос. 100
Т3-2	— "	½"	600	ст. Г: 1046 от В	межос. 100
К1-3	— "	Ø50	500	ст. Г: 1096 от В	
В1-4	ОБ-02 стиральная машина	½"	600	ст. А: 125 от Г	кран машины
К1-4	— "	Ø50	600	ст. А: 325 от Г	
В1-5	С-05 душ	½"	1200	ст. В: 541 от Г	межос. 150
Т3-3	— "	½"	1200	ст. В: 691 от Г	межос. 150
К1-5	— "	Ø50	70	ст. В: 616 от Г	сифон поддона
В1-6	С-06 унитаз подвесной	½"	250	ст. А: 466 от Г	в раме инсталляции
К1-6	— "	Ø110	220	ст. А: 316 от Г	
В1-7	С-07 умывальник	½"	600	ст. А: 216 от Б	межос. 100
Т3-4	— "	½"	600	ст. А: 316 от Б	межос. 100
К1-7	— "	Ø50	500	ст. А: 266 от Б	
В1-8	М-14 мойка кухонная	½"	600	ст. Б: 575 от А	межос. 100
Т3-5	— "	½"	600	ст. Б: 475 от А	межос. 100
К1-8	— "	Ø50	400	ст. Б: 525 от А	
В1-9	М-15 посудомоечная машина	½"	550	ст. Б: 825 от А	кран ПММ в шкафу мойки
К1-9	— "	Ø40	550	ст. Б: 725 от А	слив ПММ в шкафу мойки

Условные обозначения


- вывод В1 (код — в ведомости привязок)
- вывод Т3 (код — в ведомости привязок)
- вывод К1 (код — в ведомости привязок)
- сантехприбор по расстановке (габарит модели)
- чистовая поверхность стены (от неё привязки)
- стояк «Ст К1-N / Ст В1-N» (ГОСТ 21.601), Ø мм
- стояк Т3 не на обмере — принят в шахте рядом со Ст В1, сверить
- линия обрыва (граница фрагмента)
- А — обозначение стены А–Г (как на развёртках)

Примечания


1. Привязки выводов даны от чистовых поверхностей стен (облицовка на сторону: ванная — 24 мм (штукатурка 10 + клей 5 + плитка 9); постирочная — 15 мм (штукатурка 10 + шпаклёвка 5 (принято)); ванная мастер — 24 мм (штукатурка 10 + клей 5 + плитка 9); кухня — 22 мм (фартук: штукатурка 10 + клей 3 + плитка 9)); эти же грани — на развёртках и в раскладке плитки. Высоты — от чистого пола помещения.
2. До черновой разводки сверить по паспорту выбранного прибора (смеситель, инсталляция, сифон).
3. Горячая вода (Т3) — слева от холодной (В1), если смотреть на прибор. Допуск установки выводов: ±5 мм в группе, ±20 мм у отдельно стоящих.
4. Расчёт систем водоснабжения и канализации и подбор оборудования выполняет проектная организация; лист задаёт места и высоты выводов.
5. Посудомоечная машина М-15: кран и слив — отдельными выводами в шкафу мойки (не за машиной), до машины ≤ 1500 мм.
6. Прибор М-14 мойка кухонная, М-15 посудомоечная машина взят из расстановки мебели (по шкафу с мойкой).
7. Ст К1-3, Ст В1-3, Ст Т3-3 на обмере не показаны: положение принято, не замерено; положение сверить на объекте до разметки.
8. Стояки в коробах/шахтах не замоноличивать; стояк К1 в коробе — звукоизоляция стояка в коробе без жёсткого контакта с трубой; к арматуре и ревизиям — люк не меньше 300×400.

	Лист	№ док.	Подпись	Дата	Проект: Квартира 103 м²			М 1:50
Дизайнер	Кырлан А.С.			14.11.26	План выводов сантехники	Стадия	Лист	Листов
Проверил						П	38	129
Н. контр.								
Утв.								


План квартиры (М 1:200)

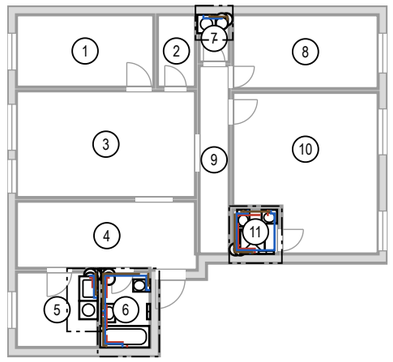


Фр. 2. Постирочная (М 1:25)

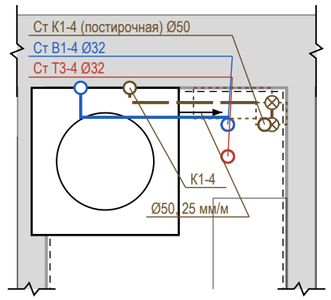


Условные обозначения

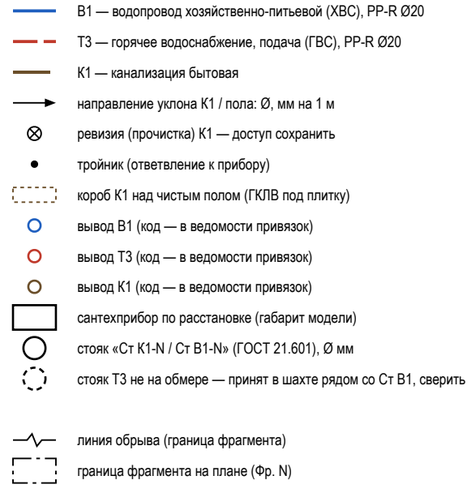


Фр. 1. Ванная (М 1:25)

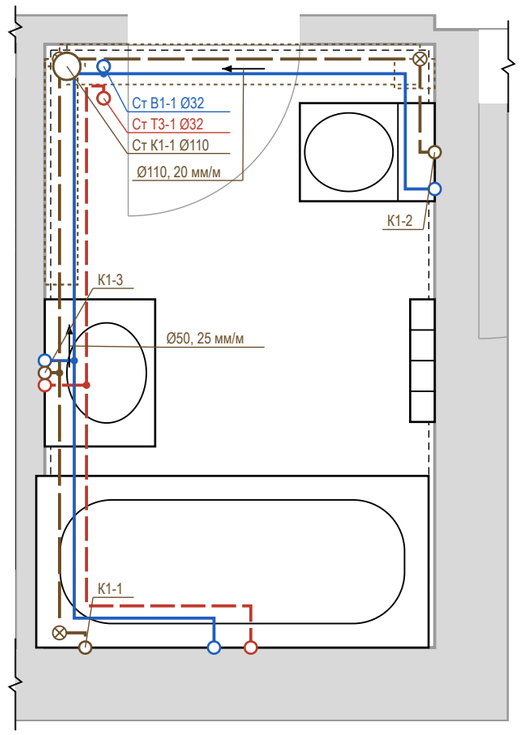

Фр. 3. Ванная мастер (М 1:25)

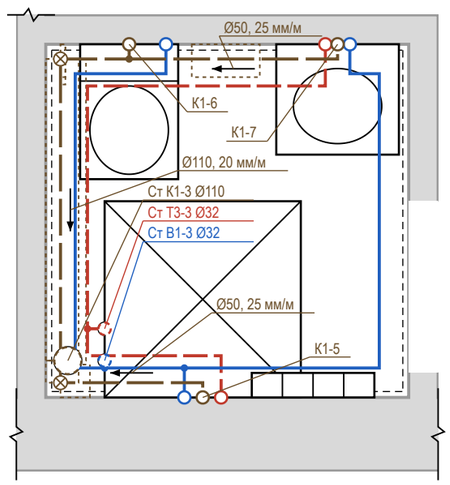

Фр. 4. Кухня (М 1:25)

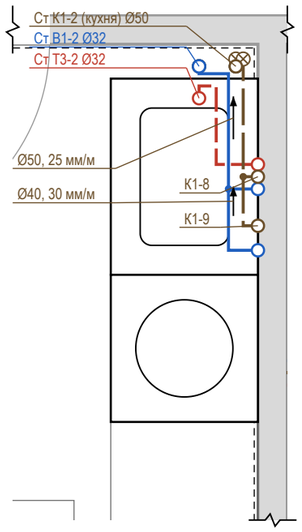


Профиль выпусков К1 (до врезки в стояк)

Выпуск	Прибор	Ø	L, м	i, мм/м	Δh, мм	Прокладка, мм
К1-2	С-02 унитаз подвесной	Ø110	1,91	20	38	под проёмом Д-5: короба нет; до решения
К1-6	С-06 унитаз подвесной	Ø110	1,60	20	32	короб 180×140
К1-1	С-01 ванна	Ø50	2,56	25	64	короб 150×110
К1-7	С-07 умывальник	Ø50	2,45	25	61	короб 150×110
К1-3	С-03 умывальник	Ø50	1,40	25	35	короб 120×110
К1-4	ОБ-02 стиральная машина	Ø50	0,76	25	19	короб 100×110
К1-5	С-05 душ	Ø50	0,76	25	19	короб 100×110
К1-8	М-14 мойка кухонная	Ø50	0,60	25	15	над полом за приборами
К1-9	М-15 посудомоечная машина	Ø40	0,80	30	24	над полом за приборами

Короб h×b: h — от чистого пола, b — от чистовой стены. Стяжка 35 мм — лист полов.

Узел ввода В1, Т3 (схема, без масштаба)

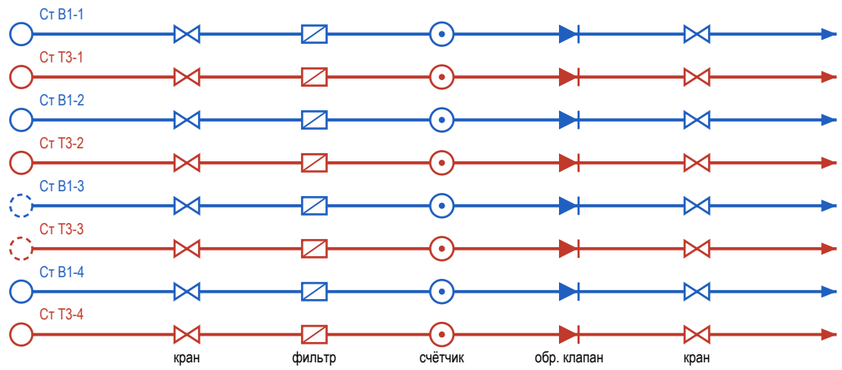

состав узла — по согласованию

⊗ Ст К1-1, Ст К1-2 (кухня), Ст К1-3, Ст К1-4 (постирочная): ревизия на стояке — люк в коробе


Примечания

1. Трассы принципиальные, построены от стояков вдоль стен помещений; фактическое положение фиксируется исполнительной схемой с привязками (фото с рулеткой) до закрытия.
2. Уклон К1 не менее 1/d и не более 150 мм/м (СП 30.13330.2020, п. 19.1), приняты практические уклоны; поворот — двумя отводами 45°, ревизия после поворота, доступ сохранить. Стояк К1 в коробе — звукоизоляция стояка в коробе, без жёсткого контакта короба с трубой.
3. Решение по К1: стяжка 35 мм не укрывает трубы (нужно Ø + Δh + 45 мм) — выпуски идут над чистым полом вдоль стен: К1-8, К1-9 — за приборами и в раме инсталляции; К1-6, К1-1, К1-7, К1-3, К1-4, К1-5 — в коробе ГКЛВ под плитку (размеры в профиле). Короба — на развёртках; отметку низа врезки в стояк замерить до черновых работ.
4. К1-2 (С-02 унитаз подвесной): трасса К1 до Ст К1-1 — под проёмом Д-5, короб там не поставить: прибор ближе к стояку, выпуск в полу с подъёмом пола или насосная установка (КНС) — решение заказчика; до решения не выполнять.
5. Состав узла ввода В1, Т3 — по согласованию: на схеме типовой узел — кран шаровой, фильтр, счётчик, обратный клапан, кран; состав и места не определены (записи реестра нет). Доступ к арматуре — через люк не меньше 300×400. Водопровод — в штробе стен или в коробах; трубы испытать давлением до закрытия (акт скрытых работ).
6. Расчёт систем, диаметры магистралей и подбор оборудования выполняет проектная организация; врезка и перенос стояков — по согласованию с управляющей организацией. Арматуру и привязки сверить по паспортам приборов.
7. Ведомость выводов (код, прибор, высота, привязка) — лист 38; на схеме — только коды.
8. Ст К1-3, Ст В1-3, Ст Т3-3 на обмере не показаны: положение принято, не замерено; положение сверить на объекте до разводки.

	Лист	№ док.	Подпись	Дата	Проект: Квартира 103 м²			
Дизайнер	Кырлан А.С.			14.11.26	Схема разводки водопровода и канализации	Стадия	Лист	Листов
Проверил						П	39	129
Н. контр.								
Утв.								

выпуск 14.11.2026 № 32d0256903 · стр. 39 из 129

Схема В1 (М 1:50)

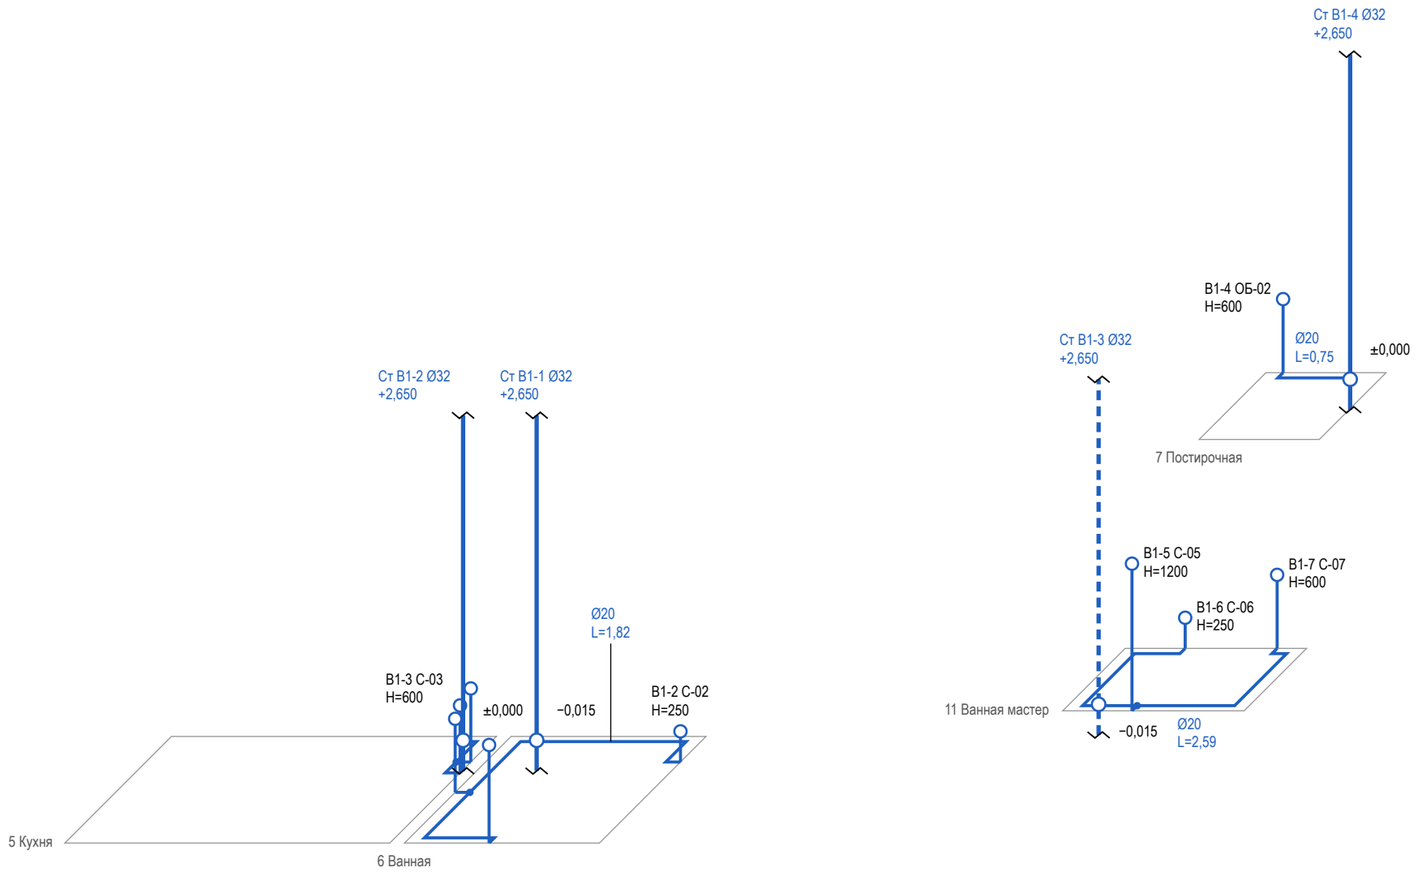

Ведомость выводов В1

Код	Прибор	H, мм	Ø, мм	Трасса, м
В1-1	С-01 ванна	800	20	3,06
В1-7	С-07 умывальник	600	20	2,59
В1-2	С-02 унитаз подвесной	250	20	1,82
В1-6	С-06 унитаз подвесной	250	20	1,81
В1-3	С-03 умывальник	600	20	0,12

Ведомость выводов В1

Код	Прибор	H, мм	Ø, мм	Трасса, м
В1-9	М-15 посудомоечная машина	550	20	0,99
В1-4	ОБ-02 стиральная машина	600	20	0,75
В1-8	М-14 мойка кухонная	600	20	0,12
В1-5	С-05 душ	1200	20	0,12

Условные обозначения


- В1 — водопровод хозяйственно-питьевой (ХВС), PP-R Ø20
- вывод В1 (код — в ведомости привязок)
- стояк «Ст К1-N / Ст В1-N» (ГОСТ 21.601), Ø мм
- стояк в плане (на отметке пола); вертикаль — стояк по высоте, разрыв — перекрытие
- тройник (ответвление к прибору)
- кран шаровой
- стояк Т3 не на обмере — принят в шахте рядом со Ст В1, сверить

Примечания

1. Схема В1 построена по тем же трассам, что план разводки: положение в плане сохранено, глубина — в масштабе ×0,5. Трассы принципиальные; фактическое положение фиксируется исполнительной схемой до закрытия.
2. Высоты H — от чистого пола помещения, мм. Отметка прокладки магистрали В1 (в стяжке, в стене или по полу) в данных не задана: участки показаны на уровне пола условно (записи реестра нет).
3. Узел ввода В1 (кран, фильтр, счётчик, обратный клапан, кран) — на схеме разводки; состав узла ввода — по согласованию. Кран шаровой — на первом участке от стояка.
4. Ст В1-3 на обмере не показаны: положение принято, не замерено; положение сверить на объекте до разводки.
5. Трубы испытать давлением до закрытия (акт скрытых работ, опрессовка по СП 73.13330.2016).
6. Диаметры, высоты выводов и места кранов — по паспортам выбранных приборов и расчёту проектной организации.
7. Расчёт систем, диаметры магистралей и подбор оборудования выполняет проектная организация.

	Лист	№ док.	Подпись	Дата	Проект: Квартира 103 м²			М 1:50
Дизайнер	Кырлан А.С.			14.11.26	Аксонометрическая схема В1 (холодное водоснабжение)	Стадия	Лист	Листов
Проверил						П	40	129
Н. контр.								
Утв.								

Схема Т3 (М 1:50)

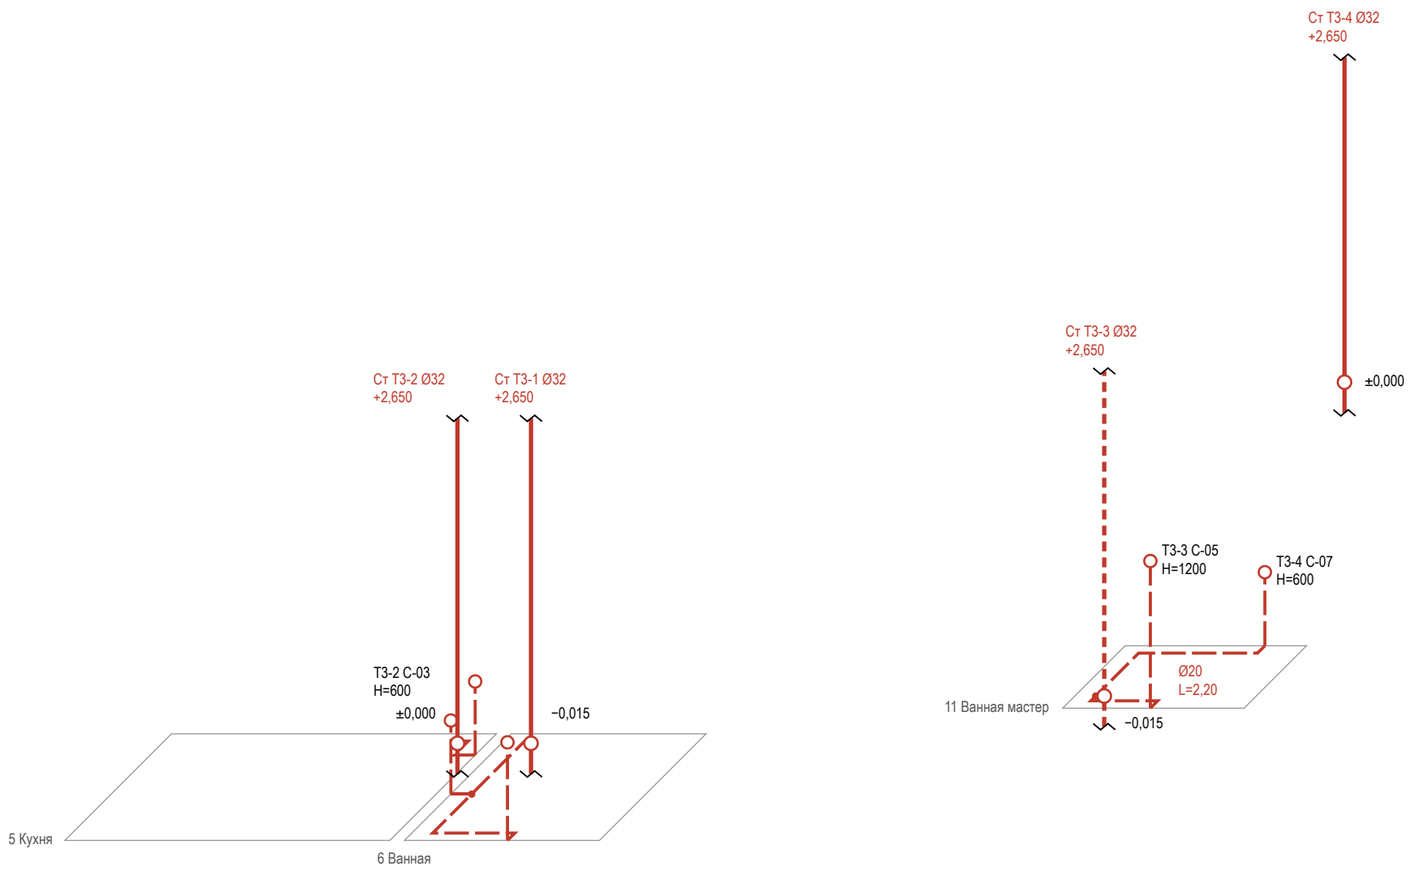

Ведомость выводов Т3

Код	Прибор	H, мм	Ø, мм	Трасса, м
Т3-1	С-01 ванна	800	20	3,08
Т3-4	С-07 умывальник	600	20	2,20
Т3-2	С-03 умывальник	600	20	0,17
Т3-3	С-05 душ	1200	20	0,82
Т3-5	М-14 мойка кухонная	600	20	0,61

Условные обозначения

- Т3 — горячее водоснабжение, подача (ГВС), PP-R Ø20
- вывод Т3 (код — в ведомости привязок)
- стояк «Ст К1-N / Ст В1-N» (ГОСТ 21.601), Ø мм
- стояк в плане (на отметке пола); вертикаль — стояк по высоте, разрыв — перекрытие
- тройник (ответвление к прибору)
- кран шаровой
- стояк Т3 не на обмере — принят в шахте рядом со Ст В1, сверить

Примечания

1. Схема Т3 построена по тем же трассам, что план разводки: положение в плане сохранено, глубина — в масштабе ×0,5. Трассы принципиальные; фактическое положение фиксируется исполнительной схемой до закрытия.
2. Высоты H — от чистого пола помещения, мм. Отметка прокладки магистрали Т3 (в стяжке, в стене или по полу) в данных не задана: участки показаны на уровне пола условно (записи реестра нет).
3. Узел ввода Т3 (кран, фильтр, счётчик, обратный клапан, кран) — на схеме разводки; состав узла ввода — по согласованию. Кран шаровой — на первом участке от стояка.
4. Циркуляция ГВС в данных не задана — циркуляционного трубопровода на схеме нет (записи реестра нет).
5. Ст Т3-3 на обмере не показаны: положение принято, не замерено; положение сверить на объекте до разводки.
6. Трубы испытать давлением до закрытия (акт скрытых работ, опрессовка по СП 73.13330.2016).
7. Диаметры, высоты выводов и места кранов — по паспортам выбранных приборов и расчёту проектной организации.
8. Расчёт систем, диаметры магистралей и подбор оборудования выполняет проектная организация.

	Лист	№ док.	Подпись	Дата
Дизайнер	Кырлан А.С.			14.11.26
Проверил				
Н. контр.				
Утв.				


Проект: Квартира 103 м² — **М 1:50**

Аксонометрическая схема Т3 (горячее водоснабжение)

Стадия	Лист	Листов
П	41	129

выпуск 14.11.2026 № 32d0256903 · стр. 41 из 129

Схема К1 (М 1:50)

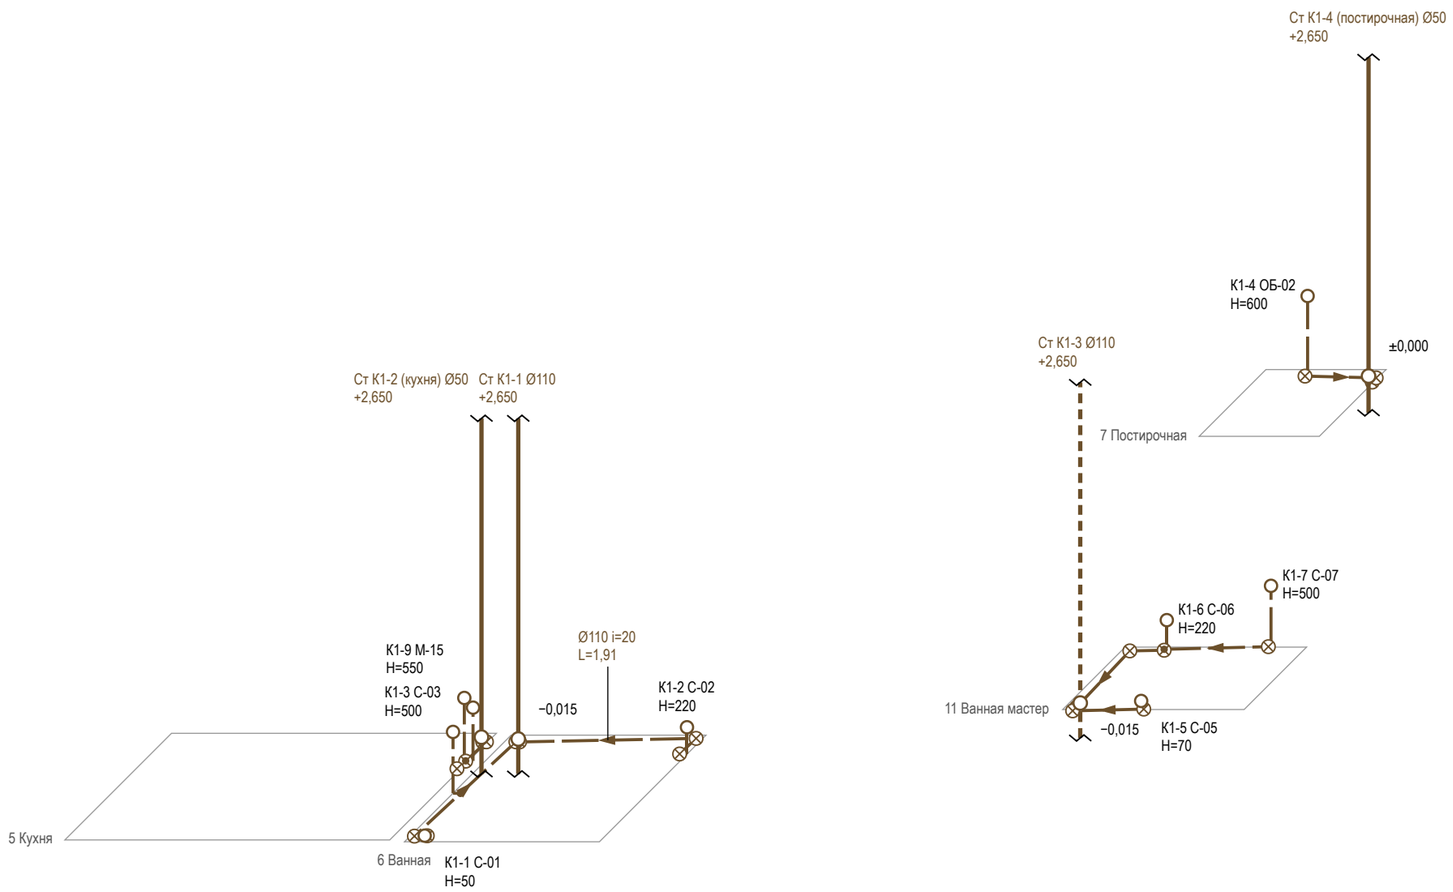

Ведомость выводов К1

Код	Прибор	H, мм	Ø, i	Трасса, м
К1-2	С-02 унитаз подвесной	220	110 i=20	1,91
К1-6	С-06 унитаз подвесной	220	110 i=20	1,60
К1-1	С-01 ванна	50	50 i=25	2,54
К1-7	С-07 умывальник	500	50 i=25	0,91
К1-3	С-03 умывальник	500	50 i=25	0,06

Ведомость выводов К1

Код	Прибор	H, мм	Ø, i	Трасса, м
К1-4	ОБ-02 стиральная машина	600	50 i=25	0,76
К1-5	С-05 душ	70	50 i=25	0,73
К1-8	М-14 мойка кухонная	400	50 i=25	0,60
К1-9	М-15 посудомоечная машина	550	40 i=30	0,26

Условные обозначения


- К1 — канализация бытовая
- вывод К1 (код — в ведомости привязок)
- стояк «Ст К1-N / Ст В1-N» (ГОСТ 21.601), Ø мм
- стояк в плане (на отметке пола); вертикаль — стояк по высоте, разрыв — перекрытие
- направление уклона К1 / пола: Ø, мм на 1 м
- ревизия (прочистка) К1 — доступ сохранить
- тройник (ответвление к прибору)
- стояк Т3 не на обмере — принят в шахте рядом со Ст В1, сверить

Примечания

1. Схема К1 построена по тем же трассам, что план разводки: положение в плане сохранено, глубина — в масштабе ×0,5. Трассы принципиальные; фактическое положение фиксируется исполнительной схемой до закрытия.
2. Отметки — от плиты перекрытия: низ трубы у врезки в стояк — отметка из данных выпуска, к прибору труба поднимается на уклон i, мм/м (уклон не менее 1/d и не более 150 мм/м, СП 30.13330.2020, п. 19.1); чистый пол — выше плиты на стяжку (высота пирога пола). Высота выпуска прибора H — от чистого пола.
3. Ревизия — на повороте и в начале участка; стояк К1 в коробе с люком — звукоизоляция стояка в коробе; поворот — двумя отводами 45°.
4. Ст К1-3 на обмере не показаны: положение принято, не замерено; положение сверить на объекте до разводки.
5. Трубы испытать давлением до закрытия (акт скрытых работ, опрессовка по СП 73.13330.2016).
6. Диаметры, высоты выводов и места кранов — по паспортам выбранных приборов и расчёту проектной организации.
7. Расчёт систем, диаметры магистралей и подбор оборудования выполняет проектная организация.

	Лист	№ док.	Подпись	Дата	Проект: Квартира 103 м²			М 1:50
Дизайнер	Кырлан А.С.			14.11.26	Аксонометрическая схема К1 (канализация)	Стадия	Лист	Листов
Проверил						П	42	129
Н. контр.								
Утв.								

Стена Б (М 1:20)

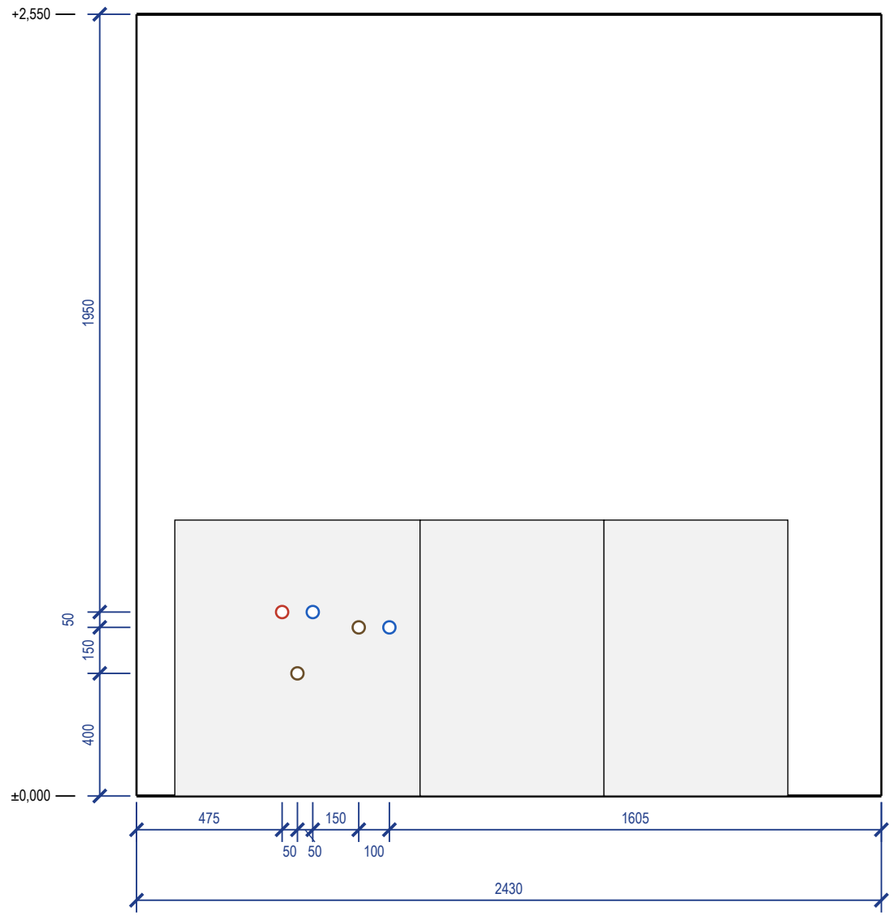

Ведомость привязок выводов (от чистого пола и угла)

Код	Прибор	Ø	H, мм	Привязка, мм
В1-8	М-14 мойка кухонная	½"	600	ст. Б: 575 от лев. угла
Т3-5	М-14 мойка кухонная	½"	600	ст. Б: 475 от лев. угла
К1-8	М-14 мойка кухонная	Ø50	400	ст. Б: 525 от лев. угла
В1-9	М-15 посудомоечная машина	½"	550	ст. Б: 825 от лев. угла
К1-9	М-15 посудомоечная машина	Ø40	550	ст. Б: 725 от лев. угла

Условные обозначения

- вывод В1 (код — в ведомости привязок)
- вывод Т3 (код — в ведомости привязок)
- вывод К1 (код — в ведомости привязок)
- сантехприбор по расстановке (габарит модели)
- дверной проём; окно — сплошной контур


Примечания

1. Габариты и высоты приборов, межосевые смесителей и места кранов — по паспортам выбранных приборов, сверяются до разметки стен.
2. Высоты H — от чистого пола помещения, мм; отметка чистого пола и потолка — у левого края вида (от ±0,000 объекта). Привязки — от левого чистового угла вида (облицовка стен вычтена), как на развёртках стен.
3. Стояки в помещении: Ст К1-2 (кухня) Ø50, Ст В1-2 Ø32, Ст Т3-2 Ø32 — положение на плане выводов; выводы подключаются к ним по схеме разводки.
4. Ревизионные люки к арматуре и ревизиям в данных не заданы: место и размер не определены (записи реестра нет).
5. Мойка, ПММ и фильтр — выводы в шкафу мойки; диаметры и положение сифона и кранов сверить по паспортам приборов и чертежам модуля.
6. Часть подписей выводов не уместилась у знака: коды и высоты — в ведомости привязок.
7. Расчёт систем водоснабжения и канализации и подбор оборудования выполняет проектная организация; лист задаёт места и высоты выводов.


	Лист	№ док.	Подпись	Дата	Проект: Квартира 103 м²			М 1:20
Дизайнер	Кырлан А.С.			14.11.26	Развёртки мокрых зон: выводы ВК. Кухня	Стадия	Лист	Листов
Проверил						П	43	129
Н. контр.								
Утв.								

выпуск 14.11.2026 № 32d0256903 · стр. 43 из 129


Стена Б (М 1:25)

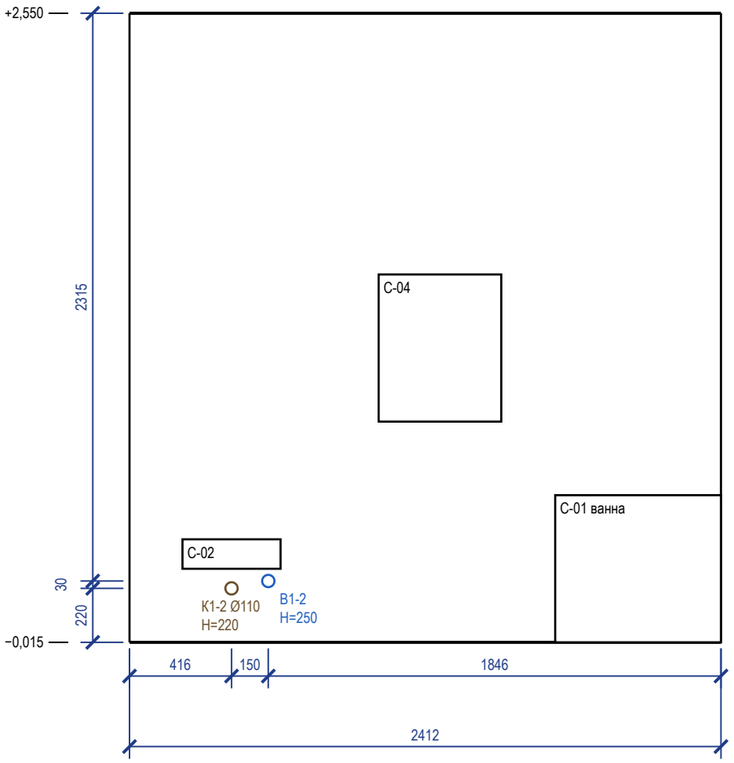

Стена В (М 1:25)

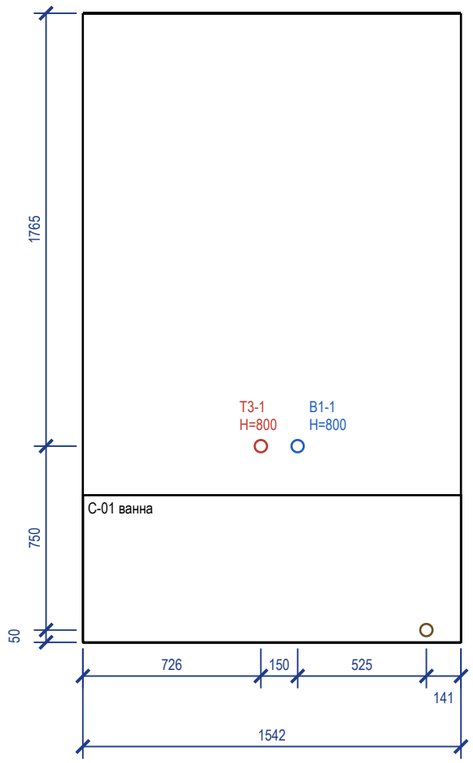

Стена Г (М 1:25)

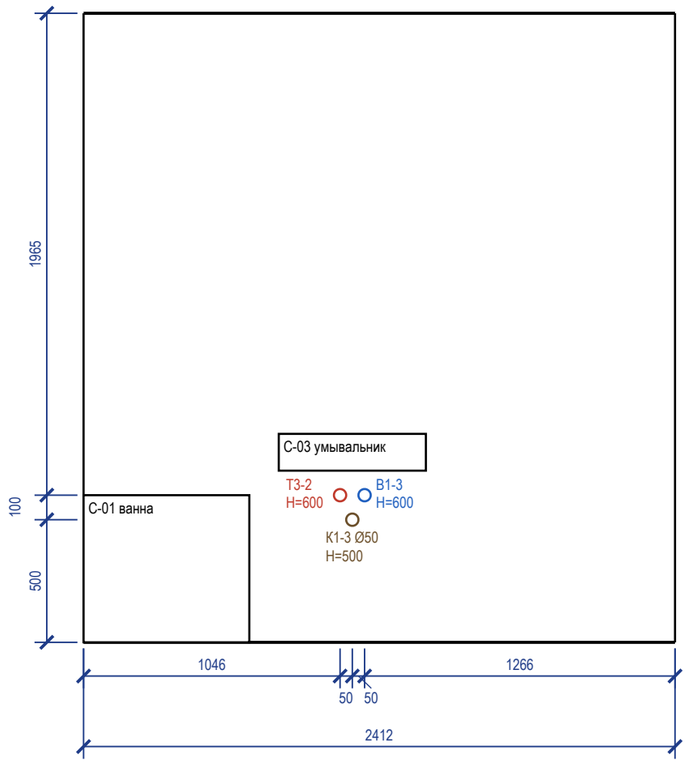

Ведомость привязок выводов (от чистого пола и угла)

Код	Прибор	Ø	H, мм	Привязка, мм
В1-2	С-02 унитаз подвесной	½"	250	ст. Б: 566 от лев. угла
К1-2	С-02 унитаз подвесной	Ø110	220	ст. Б: 416 от лев. угла
В1-1	С-01 ванна	½"	800	ст. В: 876 от лев. угла
Т3-1	С-01 ванна	½"	800	ст. В: 726 от лев. угла
К1-1	С-01 ванна	Ø50	50	ст. В: 1401 от лев. угла
В1-3	С-03 умывальник	½"	600	ст. Г: 1146 от лев. угла
Т3-2	С-03 умывальник	½"	600	ст. Г: 1046 от лев. угла
К1-3	С-03 умывальник	Ø50	500	ст. Г: 1096 от лев. угла

Условные обозначения


- вывод В1 (код — в ведомости привязок)
- вывод Т3 (код — в ведомости привязок)
- вывод К1 (код — в ведомости привязок)
- сантехприбор по расстановке (габарит модели)
- дверной проём; окно — сплошной контур

Примечания


1. Габариты и высоты приборов, межосевые смесителей и места кранов — по паспортам выбранных приборов, сверяются до разметки стен.
2. Высоты Н — от чистого пола помещения, мм; отметка чистого пола и потолка — у левого края вида (от ±0,000 объекта). Привязки — от левого чистового угла вида (облицовка стен вычтена), как на развёртках стен.
3. Стояки в помещении: Ст К1-1 Ø110, Ст В1-1 Ø32, Ст Т3-1 Ø32 — положение на плане выводов; выводы подключаются к ним по схеме разводки.
4. Ревизионные люки к арматуре и ревизиям в данных не заданы: место и размер не определены (записи реестра нет).
5. Часть подписей выводов не уместилась у знака: коды и высоты — в ведомости привязок.
6. Расчёт систем водоснабжения и канализации и подбор оборудования выполняет проектная организация; лист задаёт места и высоты выводов.

	Лист	№ док.	Подпись	Дата	Проект: Квартира 103 м²			М 1:25
Дизайнер	Кырлан А.С.			14.11.26	Развёртки мокрых зон: выводы ВК. Ванная	Стадия	Лист	Листов
Проверил						П	44	129
Н. контр.								
Утв.								

Стена А (М 1:20)

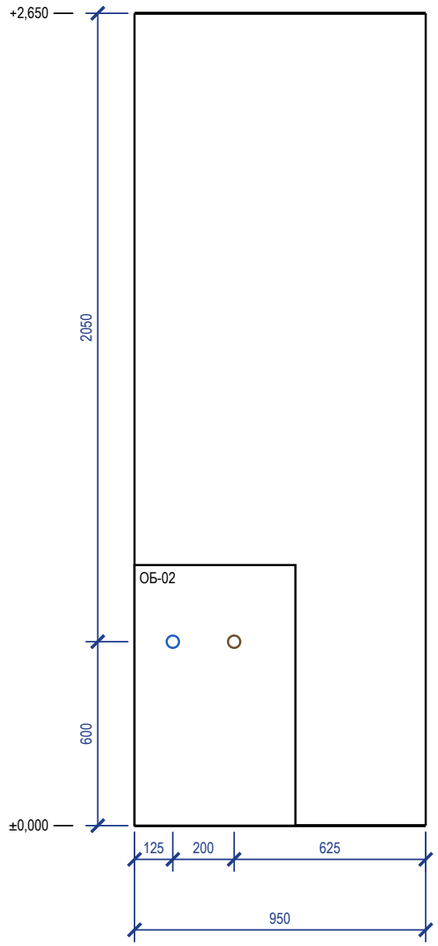

Стена Г (М 1:20)

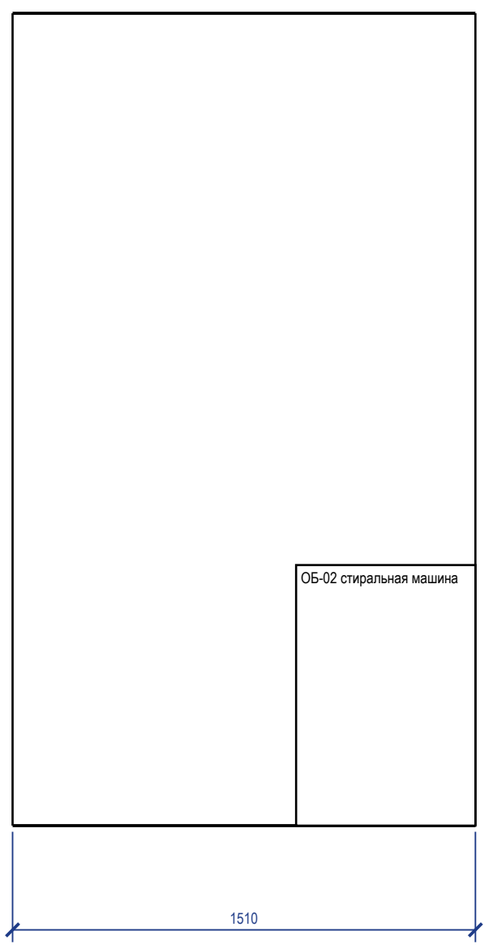

Ведомость привязок выводов (от чистого пола и угла)

Код	Прибор	Ø	H, мм	Привязка, мм
В1-4	ОБ-02 стиральная машина	½"	600	ст. А: 125 от лев. угла
К1-4	ОБ-02 стиральная машина	Ø50	600	ст. А: 325 от лев. угла

Условные обозначения

- вывод В1 (код — в ведомости привязок)
- вывод Т3 (код — в ведомости привязок)
- вывод К1 (код — в ведомости привязок)
- сантехприбор по расстановке (габарит модели)
- дверной проём; окно — сплошной контур


Примечания

1. Габариты и высоты приборов, межосевые смесителей и места кранов — по паспортам выбранных приборов, сверяются до разметки стен.
2. Высоты H — от чистого пола помещения, мм; отметка чистого пола и потолка — у левого края вида (от ±0,000 объекта). Привязки — от левого чистового угла вида (облицовка стен вычтена), как на развёртках стен.
3. Стояки в помещении: Ст К1-4 (постирочная) Ø50, Ст В1-4 Ø32, Ст Т3-4 Ø32 — положение на плане выводов; выводы подключаются к ним по схеме разводки.
4. Ревизионные люки к арматуре и ревизиям в данных не заданы: место и размер не определены (записи реестра нет).
5. Часть подписей выводов не уместилась у знака: коды и высоты — в ведомости привязок.
6. Расчёт систем водоснабжения и канализации и подбор оборудования выполняет проектная организация; лист задаёт места и высоты выводов.


	Лист	№ док.	Подпись	Дата	Проект: Квартира 103 м²		М 1:20	
Дизайнер	Кырлан А.С.			14.11.26	Развёртки мокрых зон: выводы ВК. Постирочная	Стадия	Лист	Листов
Проверил						П	45	129
Н. контр.								
Утв.								

выпуск 14.11.2026 № 32d0256903 · стр. 45 из 129


Стена А (М 1:20)

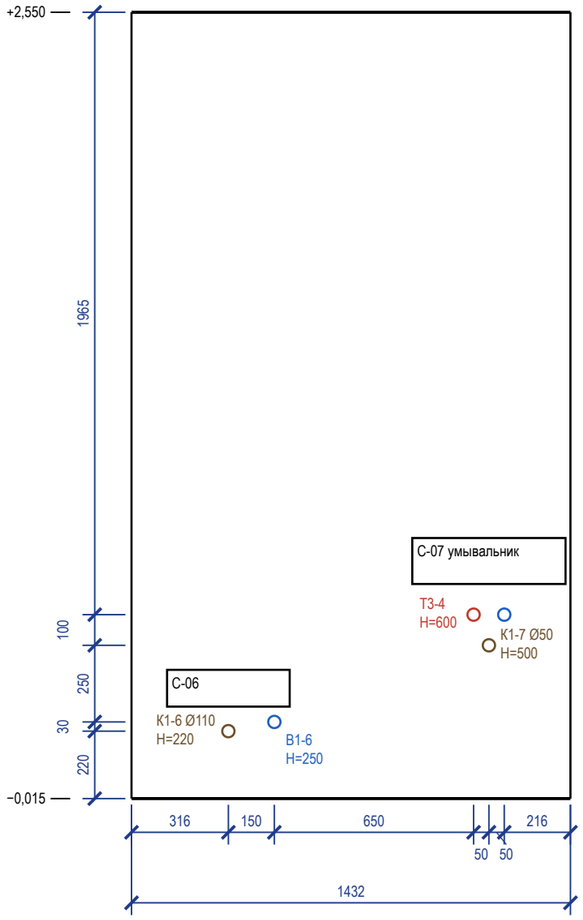

Стена Б (М 1:20)

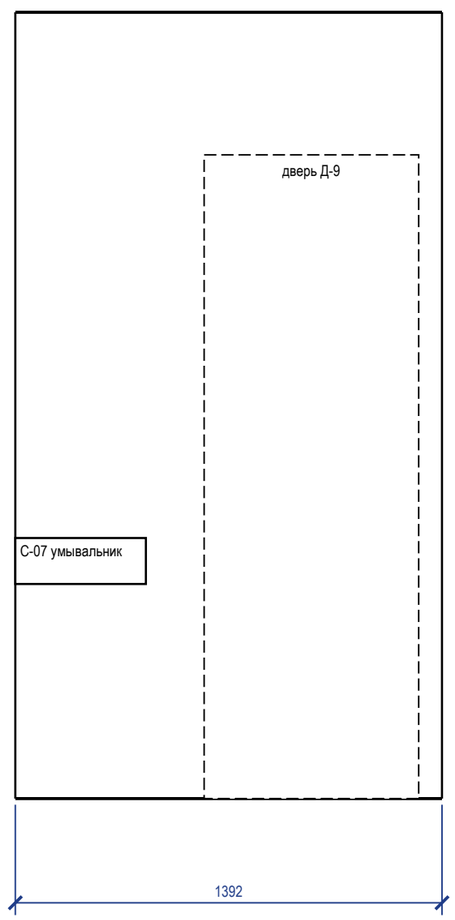

Стена В (М 1:20)

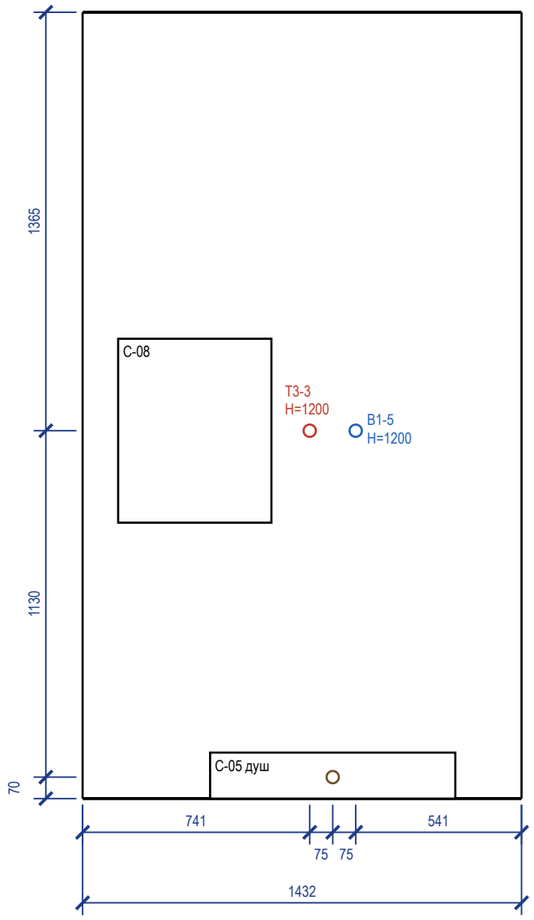

Ведомость привязок выводов (от чистого пола и угла)

Код	Прибор	Ø	H, мм	Привязка, мм
B1-6	C-06 унитаз подвесной	½"	250	ст. А: 466 от лев. угла
K1-6	C-06 унитаз подвесной	Ø110	220	ст. А: 316 от лев. угла
B1-7	C-07 умывальник	½"	600	ст. А: 1216 от лев. угла
T3-4	C-07 умывальник	½"	600	ст. А: 1116 от лев. угла

Ведомость привязок (продолжение)

Код	Прибор	Ø	H, мм	Привязка, мм
K1-7	C-07 умывальник	Ø50	500	ст. А: 1166 от лев. угла
B1-5	C-05 душ	½"	1200	ст. В: 891 от лев. угла
T3-3	C-05 душ	½"	1200	ст. В: 741 от лев. угла
K1-5	C-05 душ	Ø50	70	ст. В: 816 от лев. угла

Условные обозначения

- вывод B1 (код — в ведомости привязок)
- вывод T3 (код — в ведомости привязок)
- вывод K1 (код — в ведомости привязок)
- сантехприбор по расстановке (габарит модели)
- дверной проём; окно — сплошной контур

Примечания

1. Габариты и высоты приборов, межосевые смесителей и места кранов — по паспортам выбранных приборов, сверяются до разметки стен.
2. Высоты H — от чистого пола помещения, мм; отметка чистого пола и потолка — у левого края вида (от ±0,000 объекта). Привязки — от левого чистового угла вида (облицовка стен вычтена), как на развёртках стен.
3. Стояки в помещении: Ст K1-3 Ø110, Ст B1-3 Ø32, Ст T3-3 Ø32 — положение на плане выводов; выводы подключаются к ним по схеме разводки.
4. Ревизионные люки к арматуре и ревизиям в данных не заданы: место и размер не определены (записи реестра нет).
5. Часть подписей выводов не уместилась у знака: коды и высоты — в ведомости привязок.
6. Расчёт систем водоснабжения и канализации и подбор оборудования выполняет проектная организация; лист задаёт места и высоты выводов.

	Лист	№ док.	Подпись	Дата	Проект: Квартира 103 м²			М 1:20
Дизайнер	Кырлан А.С.			14.11.26	Развёртки мокрых зон: выводы ВК. Ванная мастер	Стадия	Лист	Листов
Проверил						П	46	129
Н. контр.								
Утв.								

выпуск 14.11.2026 № 32d0256903 · стр. 46 из 129


Поз.	Наименование и техническая характеристика	Тип, марка, обозначение документа	Код продукции	Поставщик	Ед. изм.	Кол.	Масса 1 ед., кг	Примечание
	Санитарные приборы							
1	Ванна встраиваемая акриловая 1600×700 мм, с каркасом, экраном и отверстием слив-перелив	аналог		выбор заказчика	шт	1		С-01
2	Унитаз подвесной безободковый, с сиденьем микролифт, крепёж и звукоизолирующая прокладка	Jacob Delafon Struktura EDF102-00		выбор заказчика	шт	2		С-02, С-06
3	Инсталляция для подвесного унитаза: рама высотой 1120 мм, бачок, клавиша смыва (ось клавиши 1050 мм от чистого пола)	аналог		выбор заказчика	шт	2		С-02, С-06; короб ГКЛВ
4	Умывальник подвесной 600×450 мм, с отверстием под смеситель и переливом	аналог		выбор заказчика	шт	1		С-03
5	Умывальник подвесной 500×450 мм, с отверстием под смеситель и переливом	аналог		выбор заказчика	шт	1		С-07
6	Поддон душевой низкий 800×800 мм, с сифоном и выпуском Ø50, на ножках/подиуме	аналог		выбор заказчика	шт	1		С-05
7	Мойка кухонная врезная / подстольная, с переливом, ориентир 700×480 мм — в модуле М-14 шириной 800 мм, вырез по шаблону модели	аналог		с кухонной мебелью	шт	1		М-14
8	Полотенцесушитель электрический, IP44, с терморегулятором	аналог		выбор заказчика	шт	2		С-04, С-08
	Смесители, сифоны и арматура приборов							
9	Смеситель для ванны настенный однорычажный, межосевое 150 мм, с душевым набором (лейка, шланг, держатель)	аналог		выбор заказчика	шт	1		С-01
10	Смеситель для умывальника однорычажный, с донным клапаном	аналог		выбор заказчика	шт	2		С-03, С-07
11	Душевая система скрытого монтажа с термостатом: встраиваемая часть, верхний душ, ручная лейка	аналог		выбор заказчика	шт	1		С-05; встраиваемая часть — до плитки
12	Смеситель кухонный однорычажный, высокий излив	аналог		выбор заказчика	шт	1		М-14
13	Обвязка ванны слив-перелив Ø40/50 с сифоном	аналог		выбор заказчика	шт	1		С-01
14	Сифон для умывальника бутылочный Ø32/40–50, с гофрой к выпуску	аналог		выбор заказчика	шт	2		С-03, С-07
15	Сифон для мойки Ø40/50	аналог		выбор заказчика	шт	1		М-14
16	Сифон для посудомоечной машины с обратным клапаном, на выводе слива Ø40	аналог		выбор заказчика	шт	1		М-15
17	Сифон для стиральной машины встраиваемый в стену Ø50, с обратным клапаном	аналог		выбор заказчика	шт	1		ОБ-02
18	Кран угловой ½"×½" с гибкой подводкой 40 см (умывальники, мойка)	аналог		выбор заказчика	шт	6		по 2 на прибор
19	Кран шаровой угловой ½"×¾" для подключения стиральной и посудомоечной машины	аналог		выбор заказчика	шт	2		ОБ-02, М-15
	Трубопроводы							
20	Труба полипропиленовая PP-R PN20 Ø20×3,4 (В1)	ГОСТ 32415-2013		выбор заказчика	м	19	0,17	11,4 + 5,5 + 10 %
21	Труба PP-R, армированная стекловолокном, PN20 Ø20×2,8 (Т3)	ГОСТ 32415-2013		выбор заказчика	м	12	0,15	6,9 + 3,8 + 10 %
22	Труба канализационная ПП Ø40 (К1)	ГОСТ 32414-2013		выбор заказчика	м	1		0,3 + 0,6 + 10 %
23	Труба канализационная ПП Ø50 (К1)	ГОСТ 32414-2013		выбор заказчика	м	8,5		5,6 + 2,1 + 10 %
24	Труба канализационная ПП Ø110 (К1)	ГОСТ 32414-2013		выбор заказчика	м	4,5		3,5 + 0,4 + 10 %
	Фасонные части и выводы							
25	Отвод канализационный ПП 45° Ø40	ГОСТ 32414-2013		выбор заказчика	шт	2		2 шт. на поворот
26	Отвод канализационный ПП 45° Ø50	ГОСТ 32414-2013		выбор заказчика	шт	24		2 шт. на поворот
27	Отвод канализационный ПП 45° Ø110	ГОСТ 32414-2013		выбор заказчика	шт	12		2 шт. на поворот
28	Тройник канализационный ПП 45° (врезки ветвей)	ГОСТ 32414-2013		выбор заказчика	шт	8		
29	Ревизия канализационная ПП (после поворота трассы)	ГОСТ 32414-2013		выбор заказчика	шт	11		доступ сохранить
30	Фитинги PP-R Ø20: тройники, угольники 90° (ветви и повороты В1, Т3)	ГОСТ 32415-2013		выбор заказчика	шт	42		
31	Водорозетка PP-R Ø20×½" настенная, с креплением	ГОСТ 32415-2013		выбор заказчика	шт	14		коды — лист выводов
	Узлы ввода, люки, короба							
32	Кран шаровой латунный Ду15 PN16 (отключение ввода)	аналог		выбор заказчика	шт	8		Ст В1-1, Ст Т3-1, Ст В1-2, Ст Т3-2, Ст В1-3, Ст Т3-3, Ст В1-4, Ст Т3-4
33	Фильтр сетчатый косой Ду15	аналог		выбор заказчика	шт	8		
34	Счётчик воды крыльчатый Ду15 (ХВ, ГВ), с поверкой	аналог		выбор заказчика	шт	8		пломба УК
35	Клапан обратный Ду15	аналог		выбор заказчика	шт	8		
36	Люк ревизионный нажимной под плитку 300×400 мм	аналог		выбор заказчика	шт	4		к стоякам и арматуре
37	Звукоизоляция стояка К1 в коробе: рулонный звукоизоляционный материал ≥ 10 мм, обмотка стояка на высоту этажа	аналог		выбор заказчика	м	10,8		Ст К1-1, Ст К1-2 (кухня), Ст К1-3, Ст К1-4 (постирочная)
38	Короб К1 над полом: профиль ПН/ПС, ГКЛВ 12,5 мм под плитку	аналог		выбор заказчика	м	7,8		сечение — лист разводки

Примечания

1. Форма 1 ГОСТ 21.110-2013, ширины граф изменены по п. 4.1. «Аналог» — аналог по характеристикам: модели внести до черновых работ, привязки выводов сверить по паспортам.
2. Бытовая техника не входит (показана арматура подключения), мойка — в комплекте кухни (марка — модуля кухни, как у столяра). Длины труб — трасса листа разводки + подъёмы + 10 %.
3. Стояк К1 в коробе — звукоизоляция стояка в коробе без жёсткого контакта короба с трубой.
4. Расчёт систем водоснабжения и канализации, диаметры магистралей и подбор оборудования выполняет проектная организация.

	Лист	№ док.	Подпись	Дата	Проект: Квартира 103 м²			
Дизайнер	Кырлан А.С.			14.11.26				
Проверил					Спецификация сантехнического оборудования	Стадия	Лист	Листов
Н. контр.						П	47	129
Утв.								

выпуск 14.11.2026 № 32d0256903 · стр. 47 из 129

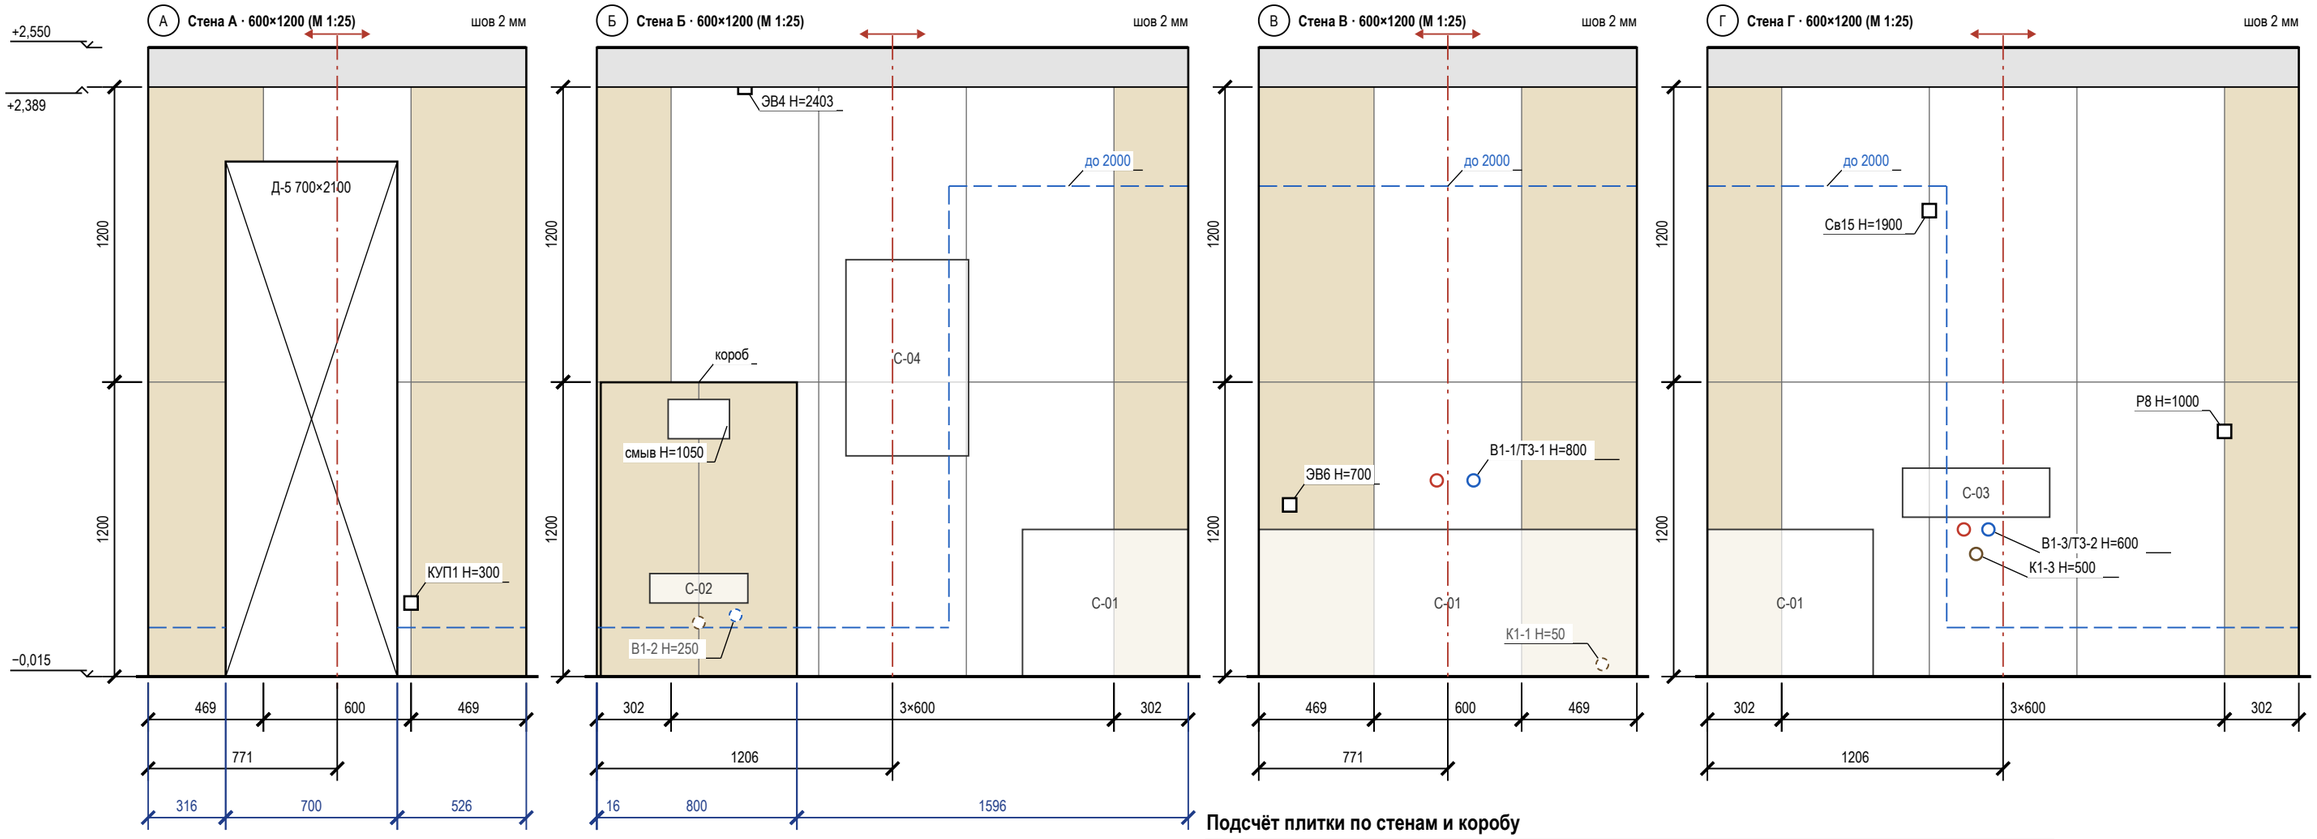

Условные обозначения

- плитка целая; тонкая линия — шов
- плитка с подрезкой (размер — на цепочке)
- ось старта; стрелки — направление укладки
- верх гидроизоляции: 200 от ЧП, в мокрой зоне — «до …»
- проём — не облицовывается
- сантехприбор: габарит, высота по практике
- короб инсталляции, в нём кнопка смыва 250×160
- вывод В1 (код — в ведомости привязок)
- вывод Т3 (код — в ведомости привязок)
- вывод К1 (код — в ведомости привязок)
- вывод за прибором / в коробе (не на сетке)
- электроточка: марка и Н — по листам ЭОМ
- отметка уровня, м: ±0,000 — чистый пол жилых помещений
- низ потолка; серая полоса — стена без плитки
- (А) обозначение стены А–Г (как на развёртках)

Примечания

1. Вид изнутри, стены по часовой стрелке А → Г. Высоты — от чистого пола (−0,015), отметки — от ±0,000. Раскладка от чистовых размеров (штукатурка 10 + клей 5 + плитка 9 мм), подрезки чистые; старт — от оси стены, ряды от пола целыми.
2. Верх плитки +2,389, потолок +2,550, зазор 161 мм: потолок ГКЛ опустить до +2,392 (шов 3 мм, герметик) — согласовать с монтажником ГКЛ; иначе профиль-окантовка, полосу окрасить в цвет потолка. Подрезной ряд 156 мм не делать.
3. Точки из таблицы сдвигов переносятся до черновой разводки (ЭОМ — по тем же числам).
4. Выводы ВК стоят по оси прибора и с прибором не двигаются — привязки по «Плану выводов сантехники» без сдвига; вне сетки (В1-1/Т3-1, В1-3/Т3-2, К1-3) отверстие в плитке коронкой по той же привязке, плитку не сдвигать.
5. За приборами и в коробе (В1-2, К1-2, К1-1) — штриховым кольцом.
6. Гидроизоляция: 200 мм от ЧП по периметру; над ванной — до 2000 и 300 мм за борт (СП 29.13330.2011, п. 7.2 — на высоту замачивания); углы — лентой; акт скрытых работ, пролив.
7. Короб 800×1200×250: лицо 399 / 399 мм от оси кнопки смыва, боковины, полка; углы — запил 45° или профиль; за коробом плитку не кладут.
8. Между коробом и углом полоса 16 мм — довести короб до угла.

Подсчёт плитки по стенам и коробу

Поверхность	L × H, мм	S, м²	Целых	Подр.	С запасом	Подрезки: край / верх, мм
стена А	1542 × 2404	2,35	0	6	7	469 / 469; целый ряд
стена Б	2412 × 2404	4,95	5	5	11	302 / 302; целый ряд
короб (ст. Б)	800×1200×250	1,76	0	6	7	лицо 399 / 399; бок. 250
стена В	1542 × 2404	3,82	2	4	7	469 / 469; целый ряд
стена Г	2412 × 2404	5,91	6	4	11	302 / 302; целый ряд
Итого		**18,80**	**13**	**25**	**43**	

Сдвиг точек под раскладку

Точка (ВК, ЭОМ)	Стена	Проект: от угла / Н	Под раскладку: от угла / Н	Сдвиг, мм
ЭВ6	В	126 / 700	169 / 700	+43 в центр плитки


	Лист	№ док.	Подпись	Дата
Дизайнер	Кырлан А.С.			14.11.26
Проверил				
Н. контр.				
Утв.				


Проект: Квартира 103 м² — **М 1:25**


Раскладка плитки. Ванная. Развёртки стен

Стадия	Лист	Листов
П	48	129

выпуск 14.11.2026 № 32d0256903 · стр. 48 из 129

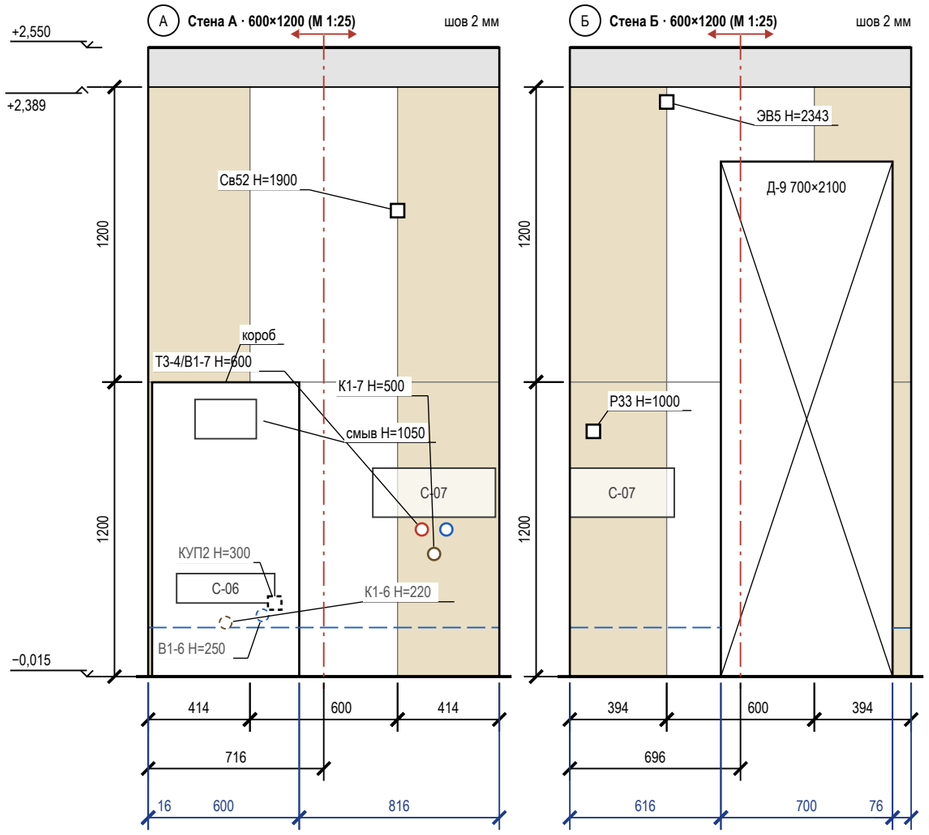

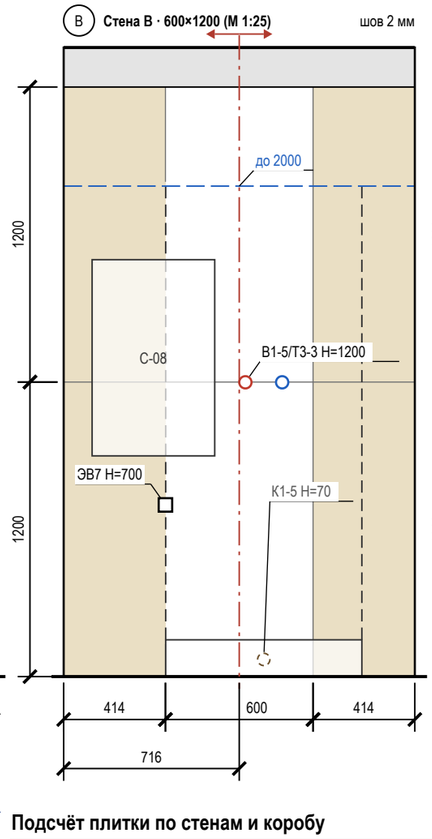

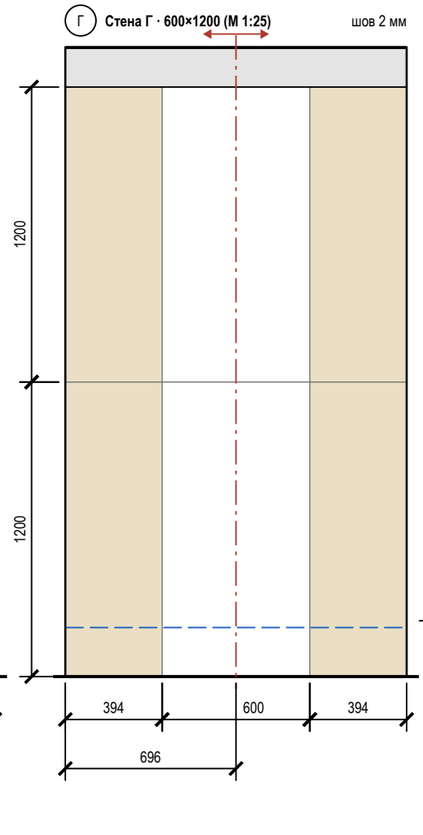

Условные обозначения

- плитка целая; тонкая линия — шов
- плитка с подрезкой (размер — на цепочке)
- ось старта; стрелки — направление укладки
- верх гидроизоляции: 200 от ЧП, в мокрой зоне — «до …»
- проём — не облицовывается
- сантехприбор: габарит, высота по практике
- граница душевой зоны (ограждение)
- короб инсталляции, в нём кнопка смыва 250×160
- вывод В1 (код — в ведомости привязок)
- вывод Т3 (код — в ведомости привязок)
- вывод К1 (код — в ведомости привязок)
- вывод за прибором / в коробе (не на сетке)
- электроточка: марка и Н — по листам ЭОМ
- отметка уровня, м: ±0,000 — чистый пол жилых помещений
- низ потолка; серая полоса — стена без плитки
- (А) обозначение стены А–Г (как на развёртках)

Подсчёт плитки по стенам и коробу

Поверхность	L × H, мм	S, м²	Целых	Подр.	С запасом	Подрезки: край / верх, мм
стена А	1432 × 2404	2,84	1	5	7	414 / 414; целый ряд
короб (ст. А)	600×1200×250	1,47	1	3	5	лицо 600; бок. 250
стена Б	1392 × 2404	1,99	0	6	7	394 / 394; целый ряд
стена В	1432 × 2404	3,56	2	4	7	414 / 414; целый ряд
стена Г	1392 × 2404	3,46	2	4	7	394 / 394; целый ряд
Итого		**13,32**	**6**	**22**	**33**	

Примечания

1. Вид изнутри, стены по часовой стрелке А → Г. Высоты — от чистого пола (−0,015), отметки — от ±0,000. Раскладка от чистовых размеров (штукатурка 10 + клей 5 + плитка 9 мм), подрезки чистые; старт — от оси стены, ряды от пола целыми.
2. Верх плитки +2,389, потолок +2,550, зазор 161 мм: потолок ГКЛ опустить до +2,392 (шов 3 мм, герметик) — согласовать с монтажником ГКЛ; иначе профиль-окантовка, полосу окрасить в цвет потолка. Подрезной ряд 156 мм не делать.
3. Открытые выводы и электроточки — на шве или в центре плитки (допуск 10 мм; плитка от 900 мм по высоте — на шве или не ближе 60 мм к нему).
4. Выводы ВК стоят по оси прибора и с прибором не двигаются — привязки по «Плану выводов сантехники» без сдвига; вне сетки (Т3-4/В1-7, К1-7, В1-5/Т3-3) — отверстие в плитке коронкой по той же привязке, плитку не сдвигать.
5. За приборами и в коробе (В1-6, К1-6, КУП2, К1-5) — штриховым кольцом.
6. Гидроизоляция: 200 мм от ЧП по периметру; у душа — до 2000 и 500 мм за поддон (СП 29.13330.2011, п. 7.2 — на высоту замачивания); углы — лентой; акт скрытых работ, пролив.
7. Короб 600×1200×250: лицо 600 мм от оси кнопки смыва, боковины, полка; углы — запил 45° или профиль; за коробом плитку не кладут.
8. Между коробом и углом полоса 16 мм — довести короб до угла.
9. Линии узора (швы плитки, складки штор, рёбра радиаторов) прерываются у знаков и выносок — просвет между линиями не менее 0,7 мм.


	Лист	№ док.	Подпись	Дата
Дизайнер	Кырлан А.С.			14.11.26
Проверил				
Н. контр.				
Утв.				

Проект: Квартира 103 м² — **М 1:25**

Раскладка плитки. Ванная мастер. Развёртки стен

Стадия	Лист	Листов
П	49	129

выпуск 14.11.2026 № 32d0256903 · стр. 49 из 129

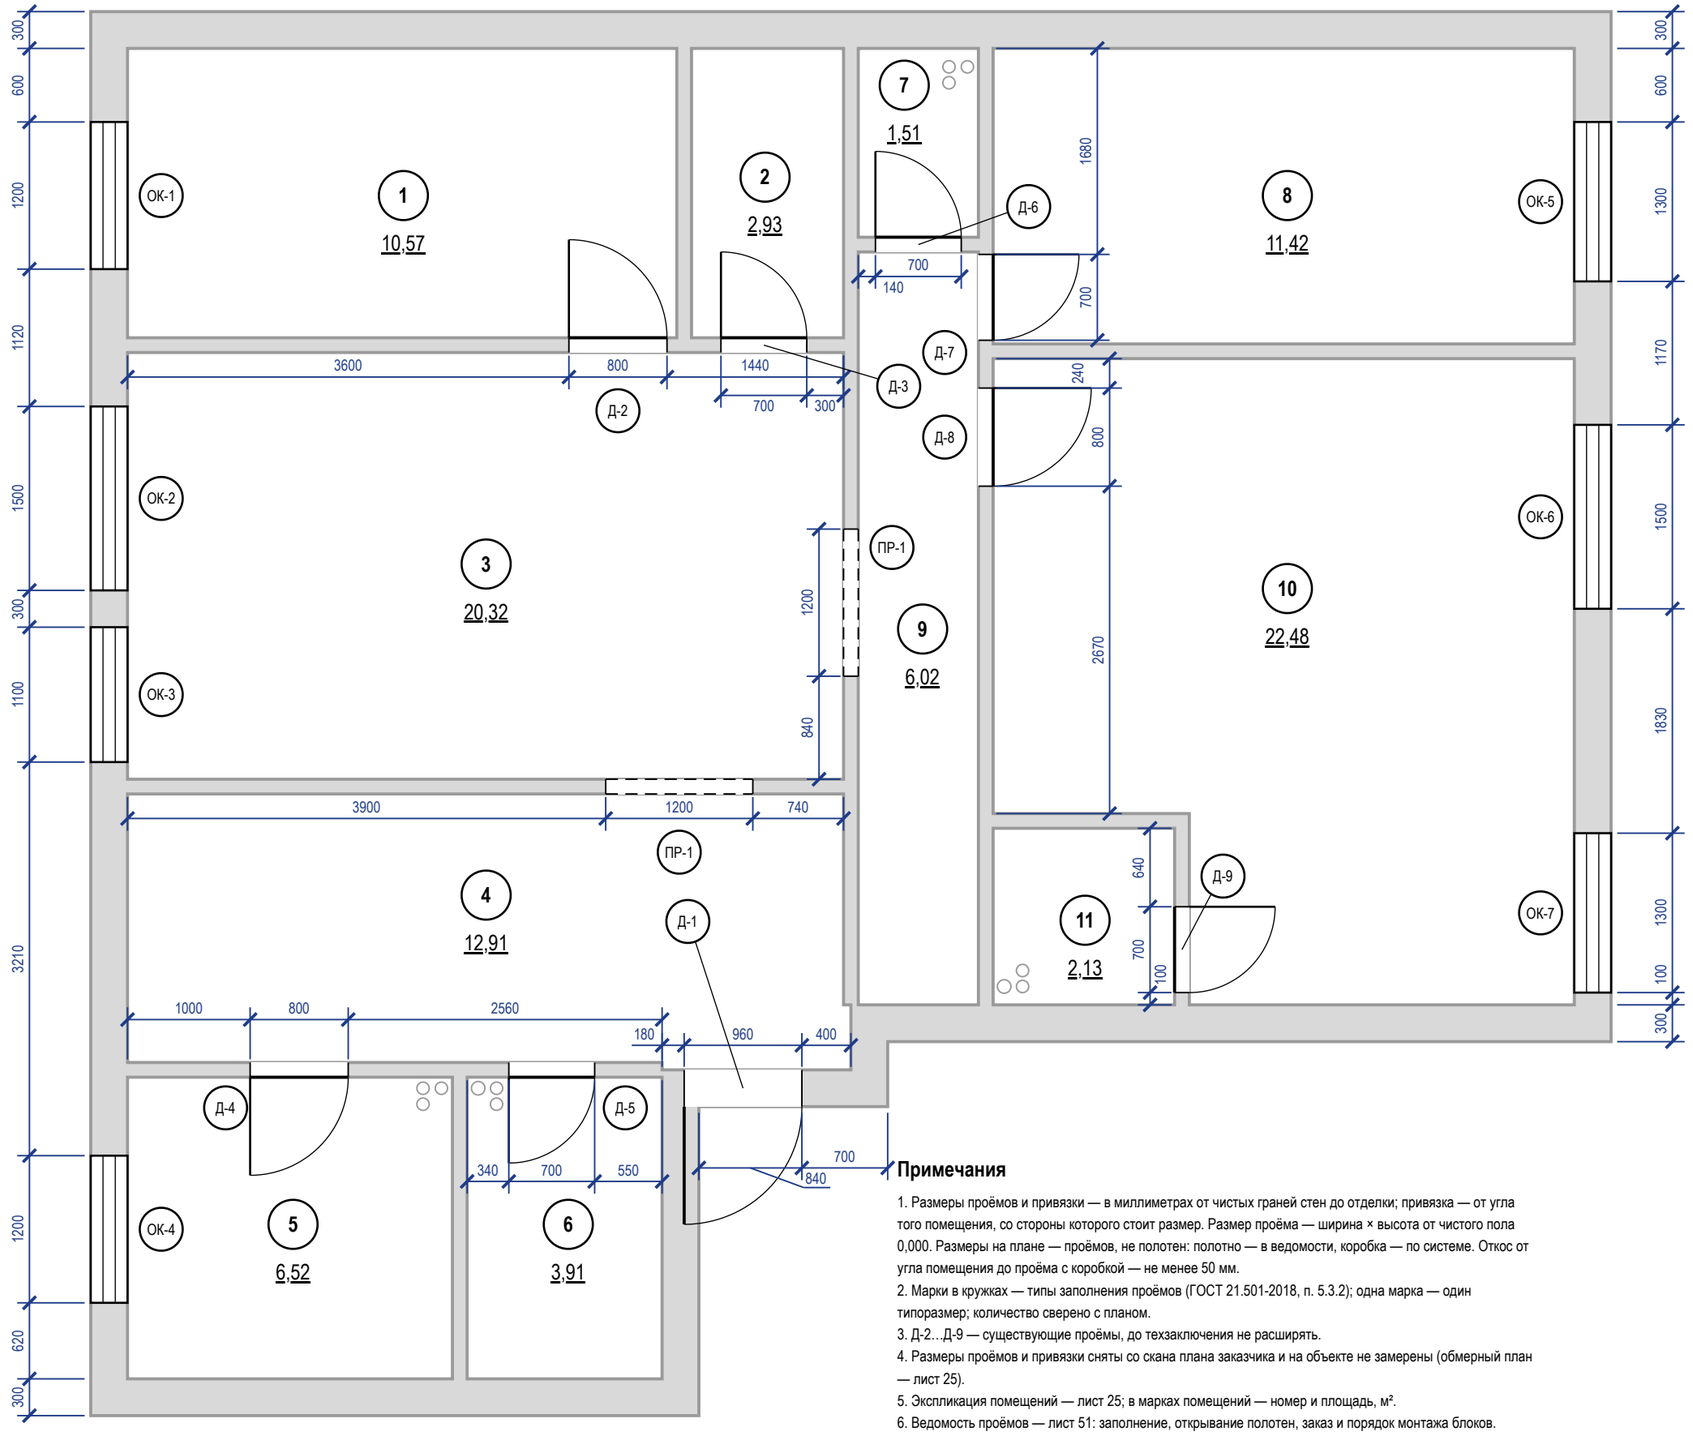

Примечания


1. Размеры проёмов и привязки — в миллиметрах от чистых граней стен до отделки; привязка — от угла того помещения, со стороны которого стоит размер. Размер проёма — ширина × высота от чистого пола 0,000. Размеры на плане — проёмов, не полотен: полотно — в ведомости, коробка — по системе. Откос от угла помещения до проёма с коробкой — не менее 50 мм.
2. Марки в кружках — типы заполнения проёмов (ГОСТ 21.501-2018, п. 5.3.2); одна марка — один типоразмер; количество сверено с планом.
3. Д-2…Д-9 — существующие проёмы, до техзаключения не расширять.
4. Размеры проёмов и привязки сняты со скана плана заказчика и на объекте не замерены (обмерный план — лист 25).
5. Экспликация помещений — лист 25; в марках помещений — номер и площадь, м².
6. Ведомость проёмов — лист 51: заполнение, открывание полотен, заказ и порядок монтажа блоков.
7. Привязка проёма к углу помещения меньше 1 мм на листе, размер на плане не показан: Д-7 — 30 мм.

	Лист	№ док.	Подпись	Дата	Проект: Квартира 103 м²			M 1:50
Дизайнер	Кырлан А.С.			14.11.26	План размещения дверей	Стадия	Лист	Листов
Проверил						П	50	129
Н. контр.								
Утв.								


Ведомость заполнения проёмов

Марка	Наименование, обозначение	Проём ш×в, мм	Полотно (расч.)	Кол.	Откр.	Отделка полотна	Фурнитура	Прим.
Д-1	Блок дверной входной, ГОСТ 31173-2016	960×2100	блок задать	1	Л	в комплекте блока	в комплекте блока (замки, глазок)	наружу
Д-2	Дверь скрытого монтажа, UNION FILO-60 Piatto	800×2100	700×2000	1	П	окраска No. 291 с двух сторон	скрытые петли 3D, магнитный замок	
Д-3	Дверь скрытого монтажа, UNION FILO-60 Piatto	700×2100	600×2000	1	П	S 0502-Y — пом. 2, No. 291 — пом. 3	скрытые петли 3D, магнитный замок	
Д-4	Дверь скрытого монтажа, UNION FILO-60 Piatto	800×2100	700×2000	1	Л	окраска No. 291 с двух сторон	скрытые петли 3D, магнитный замок	
Д-5	Дверь скрытого монтажа, UNION FILO-60 Piatto	700×2100	600×2000	1	Л	в тон облицовки — пом. 6, No. 291 — пом. 4	скрытые петли 3D, магнитный замок, фиксатор WC	порог 15
Д-6	Дверь скрытого монтажа, UNION FILO-60 Piatto	700×2100	600×2000	1	П	S 0502-Y — пом. 7, No. 291 — пом. 9	скрытые петли 3D, магнитный замок	
Д-7	Дверь скрытого монтажа, UNION FILO-60 Piatto	700×2100	600×2000	1	П	окраска No. 291 с двух сторон	скрытые петли 3D, магнитный замок	
Д-8	Дверь скрытого монтажа, UNION FILO-60 Piatto	800×2100	700×2000	1	П	окраска No. 291 с двух сторон	скрытые петли 3D, магнитный замок	
Д-9	Дверь скрытого монтажа, UNION FILO-60 Piatto	700×2100	600×2000	1	П	в тон облицовки с двух сторон	скрытые петли 3D, магнитный замок, фиксатор WC	порог 15
ПР-1	Портал без заполнения	1200×2100		2				пом. 3; б/п
ОК-1	Блок оконный, ГОСТ 23166-2021; стекло — триплекс	1200×1560		1				низ 720
ОК-2	Блок оконный, ГОСТ 23166-2021; стекло — триплекс	1500×1550		1				низ 735
ОК-3	Блок оконный, ГОСТ 23166-2021; стекло — триплекс	1100×1550		1				низ 735
ОК-4	Блок оконный, ГОСТ 23166-2021; стекло — триплекс	1200×1550		1				низ 763
ОК-5	Блок оконный, ГОСТ 23166-2021; стекло — триплекс	1300×1552		1				низ 783
ОК-6	Блок оконный, ГОСТ 23166-2021; стекло — триплекс	1500×1548		1				низ 825
ОК-7	Блок оконный, ГОСТ 23166-2021; стекло — триплекс	1300×1548		1				пом. 10; низ 825


Схемы дверных блоков (1:50) — вид со стороны открывания; вершина треугольника — сторона петель

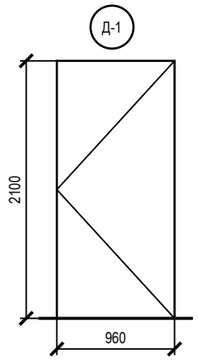


блок — по ГОСТ 31173
откр. Л

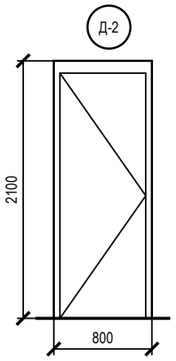


полотно 700×2000 (расч.)
откр. П

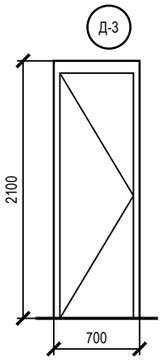


полотно 600×2000 (расч.)
откр. П

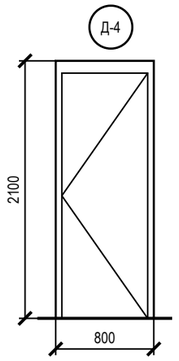


полотно 700×2000 (расч.)
откр. Л

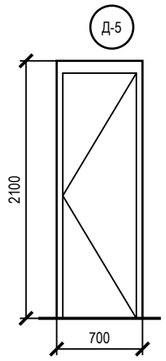


полотно 600×2000 (расч.)
откр. Л

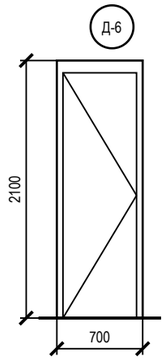


полотно 600×2000 (расч.)
откр. П

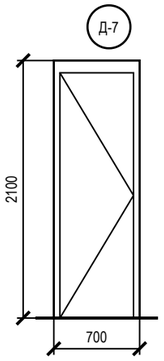


полотно 600×2000 (расч.)
откр. П

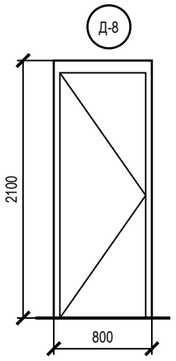

полотно 700×2000 (расч.)
откр. П

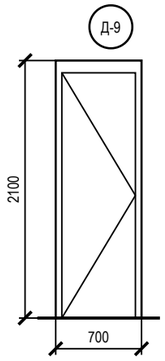

полотно 600×2000 (расч.)
откр. П

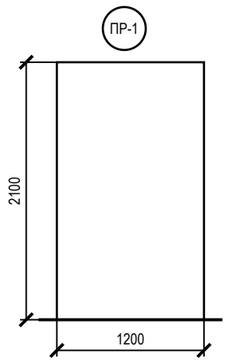


без заполнения

Примечания

1. Марки проёмов — те же, что на плане размещения дверей (лист 50); привязки проёмов — там же.
2. Открывание: Л — петли слева, П — справа, если смотреть со стороны, куда открывается полотно (на себя).
3. Остекление окон: ОК-1 (пом. 1) — триплекс; ОК-2 (пом. 3) — триплекс; ОК-3 (пом. 3) — триплекс; ОК-4 (пом. 5) — триплекс; ОК-5 (пом. 8) — триплекс; ОК-6 (пом. 10) — триплекс; ОК-7 (пом. 10) — триплекс. Тип стекла указать при заказе оконных блоков; замена на другое стекло — только по согласованию с автором проекта.
4. ОК-1, ОК-2, ОК-3, ОК-4, ОК-5, ОК-6, ОК-7: низ остекления 720 и 735 и 763 и 783 и 825 мм — ниже 900 мм от чистого пола, поэтому окно заказывать с безопасным стеклом (триплекс); ограждение проёма в проекте не задано (СП 54.13330.2022, п. 6.4.9; ГОСТ Р 56926).
5. Скрытые двери (Д-2…Д-9): проём замерить в чистоте; блок заказать до штукатурки (≈ 30 дн.), короб ставить до штукатурки; полотно навесить после чистовой отделки, красить в цвет стен. Порядок — практика монтажа, изготовитель подтверждает.
6. Полотно «расч.» — по проёму и ряду изделия с запасом по каталогам, заказ — по таблице проёмов модели; Д-2…Д-9: проём 2100, а под полотно 2000 по каталогам нужен 2050–2080, под 2100 — 2150–2180: высоту проёма — по модели; Д-1: входной блок по ГОСТ 31173-2016 — задать при выборе блока.

	Лист	№ док.	Подпись	Дата	Проект: Квартира 103 м²			
Дизайнер	Кырлан А.С.			14.11.26				
Проверил					Ведомость заполнения проёмов	Стадия	Лист	Листов
Н. контр.						П	51	129
Утв.								

выпуск 14.11.2026 № 32d0256903 · стр. 51 из 129

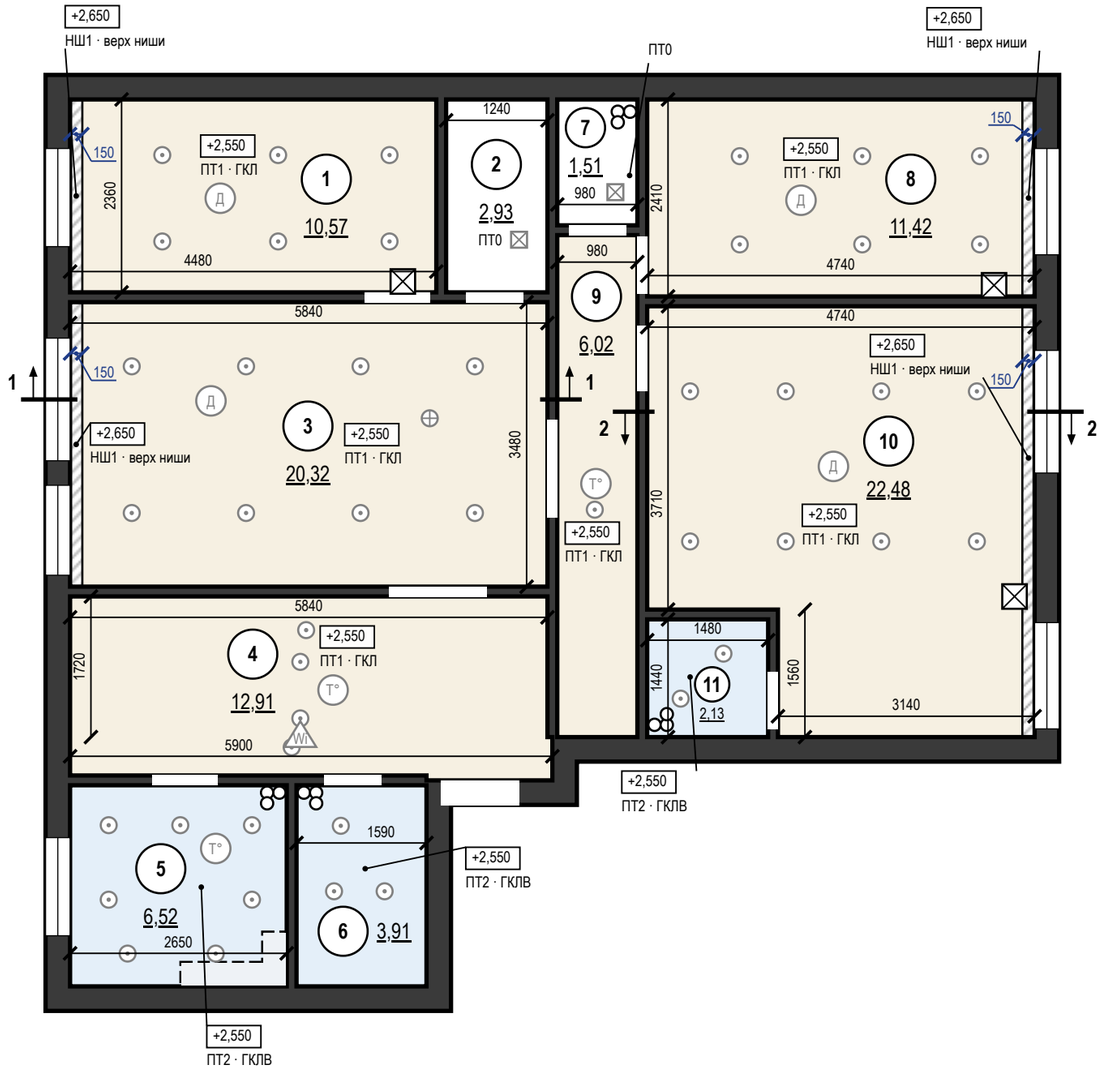

Ведомость потолков

Пом.	Марка	Конструкция	Низ / верх ниши	S, м²	Q
1	ПТ1	ГКЛ П113	+2,550	10,22	Q3
1	НШ1	ниша под шторы 150×100	+2,650	0,35	
2, 7	ПТ0	Существующий потолок, окраска	+2,650	4,44	
3	ПТ1	ГКЛ П113	+2,550	19,80	Q3
3	НШ1	ниша под шторы 150×100	+2,650	0,52	
4	ПТ1	ГКЛ П113	+2,550	12,91	Q3
5	ПТ2	ГКЛВ П113	+2,550	6,52	Q3
6	ПТ2	То же	+2,550	3,91	Q3
8	ПТ1	ГКЛ П113	+2,550	11,06	Q3
8	НШ1	ниша под шторы 150×100	+2,650	0,36	
9	ПТ1	ГКЛ П113	+2,550	6,02	Q3
10	ПТ1	То же	+2,550	21,69	Q3
10	НШ1	ниша под шторы 150×100	+2,650	0,79	
11	ПТ2	ГКЛВ П113	+2,550	2,13	Q3
		Итого		**100,72**	


Примечания

1. За отметку ±0,000 принят уровень чистого пола сухих помещений (готовое покрытие), а не существующего пола; пол пом. 6, 11 — −0,015; верх плиты перекрытия −0,064 — расчётный по пирогу пола, не замерен; существующий пол снимается до плиты, его отметка не замерена. Отметки в прямоугольниках — низ потолка; низ перекрытия +2,650. Марка потолка — одна конструкция и отметка на весь альбом.
2. Размеры помещений в свету (ширина × длина, мм), не поместившиеся на плане: пом. 2 — 1240 × 2360; пом. 4 — 5840 × 1720, 5900 × 470, 1540 × 60; пом. 5 — 2650 × 2460; пом. 6 — 1590 × 2460; пом. 7 — 980 × 1540; пом. 9 — 980 × 6140.
3. Потолки ГКЛ — каркасная система П113: подвесы через 1000 (с запасом: СП 163, табл. 14 — до 1100 при 0,15 кН/м²), несущие профили через 500, основные через 1200 мм; листы — поперёк несущих профилей. В помещениях 5, 6, 11 — ГКЛВ на оцинкованном каркасе.
4. Ниши под шторы 150×100 мм — на всю длину стены с окном; карниз — на закладной до обшивки (узел 1, лист 53).
5. Примыкание к стенам: теневой шов 15 мм, техзазор 3 мм — пом. 1, 3, 4, 5, 8, 9, 10, по стенам, выровненным штукатуркой (узел 1); пом. 6, 11 — разделительная лента.
6. Светильники и потолочные устройства — подложка с планов освещения, слаботочных систем и вентиляции (положение — по ним); вырезы и закладные — по ведомости на листе, до обшивки; отверстия не совмещать с профилями, глубина корпуса светильника до 70 мм.
7. Разрезы 1–1, 2–2 — на листе 53; высоты мебели и дверных блоков сверены с низом потолка в разрезах.
8. Шпаклевание ГКЛ и условия приёмки — Q3: рассеянный дневной свет, осмотр с 2 м; боковой свет не оценивается.
9. Ведомость вырезов и закладных в потолке — на листе 54; вырезы и закладные — до обшивки.
10. Пом. 5: короб воздуховода кухонной вытяжки ГКЛ 300×130 мм (ширина от стены × высота), низ +2,520, длина 1,37 м — по трассе плана вентиляции, вдоль стен до входа в канал; под плоский воздуховод 200×60 (сечение ≈ Ø125): круглый Ø125 в коробе 200 мм опустил бы кухню ниже 2,5 м — сечение подтверждает раздел ОВ; каркас ПН 28×27 по стене и плите, ПП 60×27, лист ГКЛ 12,5.
11. Люки ревизии 300×300 мм — по центру блоков питания LED (БП2, БП5, БП6; координаты — план освещения).
12. ПТ0 — пом. 2, 7: существующий потолок, окраска, без подвесного потолка, низ +2,650; материал и цвет — по ведомости отделки.
13. Сечения потолков М 1:10: пом. 1 — 1.1, 1.2 (лист 55); пом. 3 — 1.1, 1.2 (лист 55); пом. 8 — 1.1, 1.2 (лист 55); пом. 10 — 1.1, 1.2 (лист 55).

	Лист	№ док.	Подпись	Дата	Проект: Квартира 103 м²		М 1:75	
Дизайнер	Кырлан А.С.			14.11.26				
Проверил					План потолков	Стадия	Лист	Листов
Н. контр.						П	52	129
Утв.								


Разрез 1–1 (М 1:40)

Пом. 3 Гостиная-столовая; линия разреза — план потолков, лист 52

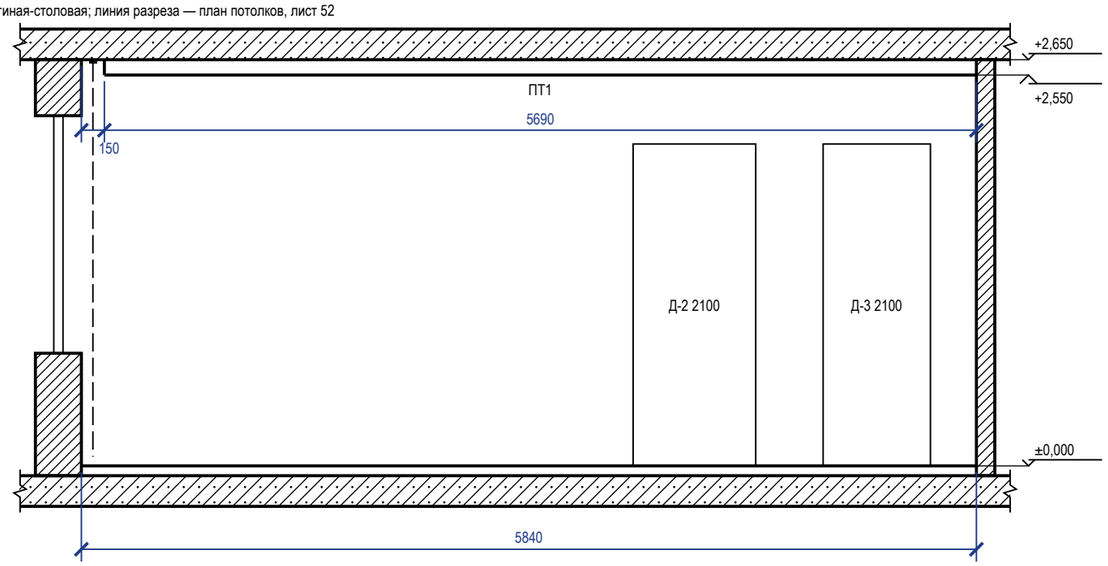

Разрез 2–2 (М 1:40)

Пом. 10 Спальня мастер; линия разреза — план потолков, лист 52

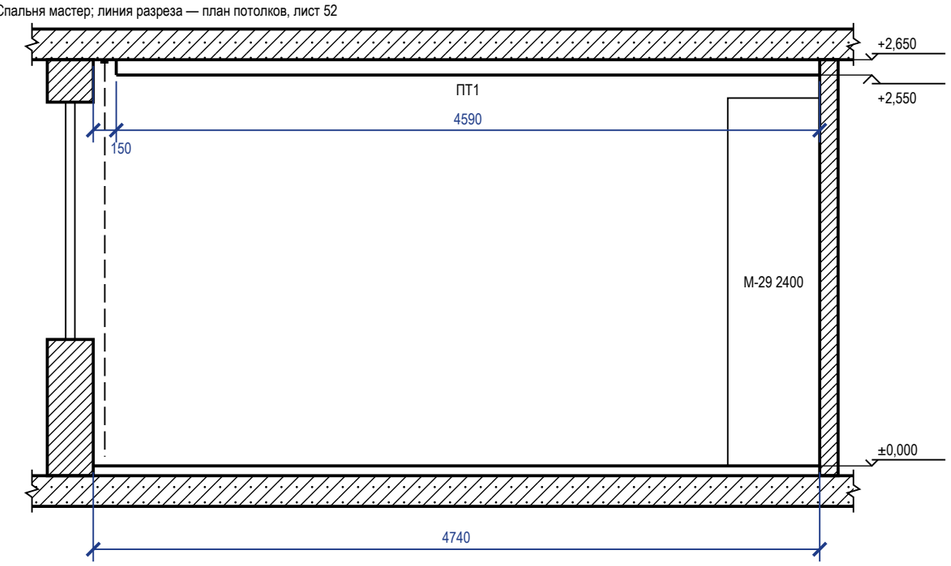

1 Ниша под шторы (М 1:10)

Пом. 1, 3, 8, 10; без подсветки; закладные под карниз — до обшивки

1 — карниз (шина), высота с верхом портьеры 80 мм
2 — стенка ниши — ГКЛ 12,5
3 — ПП 60×27 — каркас короба
4 — низ короба нижнего уровня — ГКЛ 12,5
5 — портьера
6 — стена с окном

Условные обозначения

- плита перекрытия в сечении
- стена в сечении
- потолок ГКЛ в сечении; под линией — марка потолка (план потолков)
- мебель и дверные проёмы за секущей плоскостью; число — марка и верх от чистого пола, мм
- портьера в нише под шторы

Примечания

1. Разрезы — по линиям 1–1, 2–2 на плане потолков (лист 52). Отметки — от ±0,000 чистого пола, м; размеры — мм.
2. Высоты мебели и дверных блоков за секущей плоскостью сверены с низом потолка над ними: верх ниже низа короба и поля.
3. ГКЛ 12,5 мм по каркасу П113. Ниша под шторы — на всю длину стены с окном, карниз на закладной до обшивки (узел 1 — на этом листе).
4. Толщины плит перекрытия и пирога пола показаны условно.
5. Сечения потолков по помещениям М 1:10 (отметки помещения, профили, подвесы, крепёж, изделия) — лист 55.
6. Ведомость объёмов потолков (лист ГКЛ, профиль, подвесы, лента, блоки питания, люки) — на листе 55.

	Лист	№ док.	Подпись	Дата
Дизайнер	Кырлан А.С.			14.11.26
Проверил				
Н. контр.				
Утв.				

Проект: Квартира 103 м² — **М 1:40; 1:10**

Разрезы и узлы потолков

Стадия	Лист	Листов
П	53	129

выпуск 14.11.2026 № 32d0256903 · стр. 53 из 129

Ведомость вырезов и закладных в потолке

Марка	Устройство	Кол.	Пом.
	Светильник встраиваемый (марки — план освещения)	46	1, 3, 4, 5, 6, 8, 9, 10, 11
	Светильник накладной (марки — план освещения)	2	2, 7
	Светильник подвесной (марки — план освещения)	1	3
ИП2, ИП1, ИП7, ИП8	Извещатель дымовой	4	1, 3, 8, 10
ИП3, ИП4, ИП6	Извещатель тепловой	3	4, 5, 9
AP1	Точка доступа Wi-Fi, PoE	1	4
	Люк ревизии 300×300	3	1, 8, 10

Примечания


1. ГКЛ 12,5 мм по каркасу П113; узлы коробов и ниш под шторы: узел 1 — лист 53; условные обозначения разрезов — на листе 53.
2. Ведомость вырезов и закладных в потолке — к плану потолков (лист 52): вырезы и закладные — до обшивки, марки светильников — по плану освещения.

выпуск 14.11.2026 № 32d0256903 · стр. 54 из 129

	Лист	№ док.	Подпись	Дата	Проект: Квартира 103 м²			
Дизайнер	Кырлан А.С.			14.11.26	Разрезы и узлы потолков (продолжение)	Стадия	Лист	Листов
Проверил						П	54	129
Н. контр.								
Утв.								

Сечение 1.1. Ниша под шторы (М 1:10)

Пом. 1 Кабинет-библиотека, 3 Гостиная-столовая, 8 Спальня 2, 10 Спальня мастер; без подсветки; закладные под карниз — до обшивки

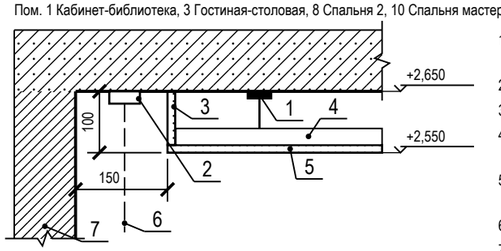

1 — анкер-клин к плите — по одному на подвес; подвес прямой, шаг 1000 мм

2 — карниз (шина), высота с верхом портьеры 80 мм

3 — стенка ниши — ГКЛ 12,5

4 — ПП 60×27 — каркас короба, основные через 1200 мм; соединители одноуровневые, шурупы LN 3,5×9


5 — низ короба нижнего уровня — ГКЛ 12,5; шурупы TN 3,5×25 через 170 мм

6 — портьера

7 — стена с окном

Сечение 1.2. Примыкание потолка к стене (М 1:10)

Пом. 1 Кабинет-библиотека, 3 Гостиная-столовая, 8 Спальня 2, 10 Спальня мастер; примыкание — теневой шов

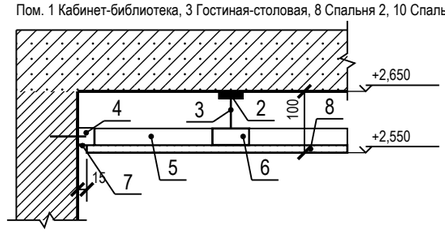

1 — плита перекрытия

2 — анкер-клин к плите — по одному на подвес

3 — подвес прямой, шаг 1000 мм

4 — ПН 28×27 по периметру — дюбель-гвоздь через ≤ 500 мм, не менее 3 на профиль

5 — ПП 60×27 несущий (вид) через 500 мм, в ПН

6 — ПП 60×27 основной (сечение) через 1200 мм; соединители одноуровневые, шурупы LN 3,5×9

7 — теневой профиль: шов 15 мм, зазор 3 мм; стена под шов выровнена

8 — ГКЛ 12,5 по П113; шурупы TN 3,5×25 через 170 мм

Ведомость объёмов потолков

Позиция	Ед.	Кол.	Пом.
Лист ГКЛ 12,5	м²	85,08	1, 3, 4, 8, 9, 10
Лист ГКЛВ 12,5	м²	12,56	5, 6, 11
Борта и карнизы (входят в площади листов выше)	м²	1,36	1, 3, 8, 10
Профиль ПП 60×27	м	276,03	1, 3, 4, 5, 6, 8, 9, 10, 11
Профиль ПН 28×27	м	148,38	1, 3, 4, 5, 6, 8, 9, 10, 11
Подвес прямой	шт.	84	1, 3, 4, 5, 6, 8, 9, 10, 11
Анкер-клин к плите	шт.	84	1, 3, 4, 5, 6, 8, 9, 10, 11
Шуруп TN 3,5×25	шт.	2246	1, 3, 4, 5, 6, 8, 9, 10, 11
Лента армирующая для швов	м	117,17	1, 3, 4, 5, 6, 8, 9, 10, 11
Шпаклёвка для швов	кг	39,06	1, 3, 4, 5, 6, 8, 9, 10, 11
Грунтовка (швы)	л	9,76	1, 3, 4, 5, 6, 8, 9, 10, 11
Лента разделительная по периметру	м	121,34	1, 3, 4, 5, 6, 8, 9, 10, 11
Сплошная шпаклёвка и окраска (площадь развёртки)	м²	97,64	1, 3, 4, 5, 6, 8, 9, 10, 11
Люк ревизии	шт.	3	1, 8, 10

Примечания


1. Сечения потолков М 1:10 по помещениям с нишами LED и нишами под шторы: отметки и размеры этого помещения от ±0,000 чистого пола (м, мм). Положение — по плану потолков (лист 52): короб и ниша LED — по линиям ленты, ниша под шторы — у стены с окном; типовые узлы по группам помещений — на листе 53.
2. Крепёж: подвес прямой к плите на анкер-клине — по одному на подвес (Knauf П113); ПН к стенам — дюбель-гвоздь через ≤ 500 мм, не менее 3 на профиль (серия 1.045.9-2.08); лист 12,5 — шурупы TN 3,5×25 через 170 мм (СП 163, табл. 15); профили между собой — соединители одноуровневые, шурупы LN 3,5×9.
3. Изделие карниза, профиля LED и галтели подписано артикулом из данных; где артикул не выбран, сечение дано по габаритам из данных (ширина и глубина ниши, щель под свет), изделие подбирается по ним.
4. Ведомость объёмов — по геометрии плана потолков: Лист ГКЛ 12,5 — плоскости уровней + борта (без арочных участков); Лист ГКЛВ 12,5 — плоскости уровней + борта; Борта и карнизы — длина перепада × перепад; Профиль ПП 60×27 — S × (1/шаг несущ. + 1/шаг осн.) + стойки бортов; Профиль ПН 28×27 — периметр стен + 2 × перепады + карнизы; Подвес прямой — по раскладке: S уровня / (шаг осн. × шаг подвесов), пояс уже шага — ряд вдоль пояса, фигура — по контуру; шаг подвесов — не больше табл. 14 СП 163; Анкер-клин к плите — по одному на подвес (Knauf П113); Шуруп TN 3,5×25 — 23 шт./м² (Knauf П113, табл. 2 альбома П 11); Лента армирующая для швов — 1,2 м/м² листа (Knauf); Шпаклёвка для швов — 0,4 кг/м² листа, только швы (Knauf); Грунтовка (швы) — 0,1 л/м² листа, только швы (Knauf); Лента разделительная по периметру — периметр стен под потолком ГКЛ; Сплошная шпаклёвка и окраска (площадь развёртки) — плоскости + борта; расход — по паспорту материала (норма расхода на сплошной слой не подтверждена); Люк ревизии — план потолков; без запаса на подрезку (при закупке листа: ×1,075 при S > 20 м², ×1,175 — 10–20 м², ×1,275 — < 10 м²).

	Лист	№ док.	Подпись	Дата	Проект: Квартира 103 м²			М 1:10
Дизайнер	Кырлан А.С.			14.11.26	Сечения потолков М 1:10	Стадия	Лист	Листов
Проверил						П	55	129
Н. контр.								
Утв.								

выпуск 14.11.2026 № 32d0256903 · стр. 55 из 129

Условные обозначения

- автоматический выключатель, QF — номер группы, характеристика и ток
- УЗО (с автоматом — дифавтомат): ток утечки, тип AC/A
- Wh — счётчик электроэнергии
- шина: L — фаза, N — нулевой рабочий, PE — защитный проводник
- УЗИП (ограничитель перенапряжений), FV — марка
- ГЗШ — главная заземляющая шина; штрихпунктир — проводник основной системы уравнивания потенциалов (ОСУП)
- резервный аппарат (не менее 20 % групп)

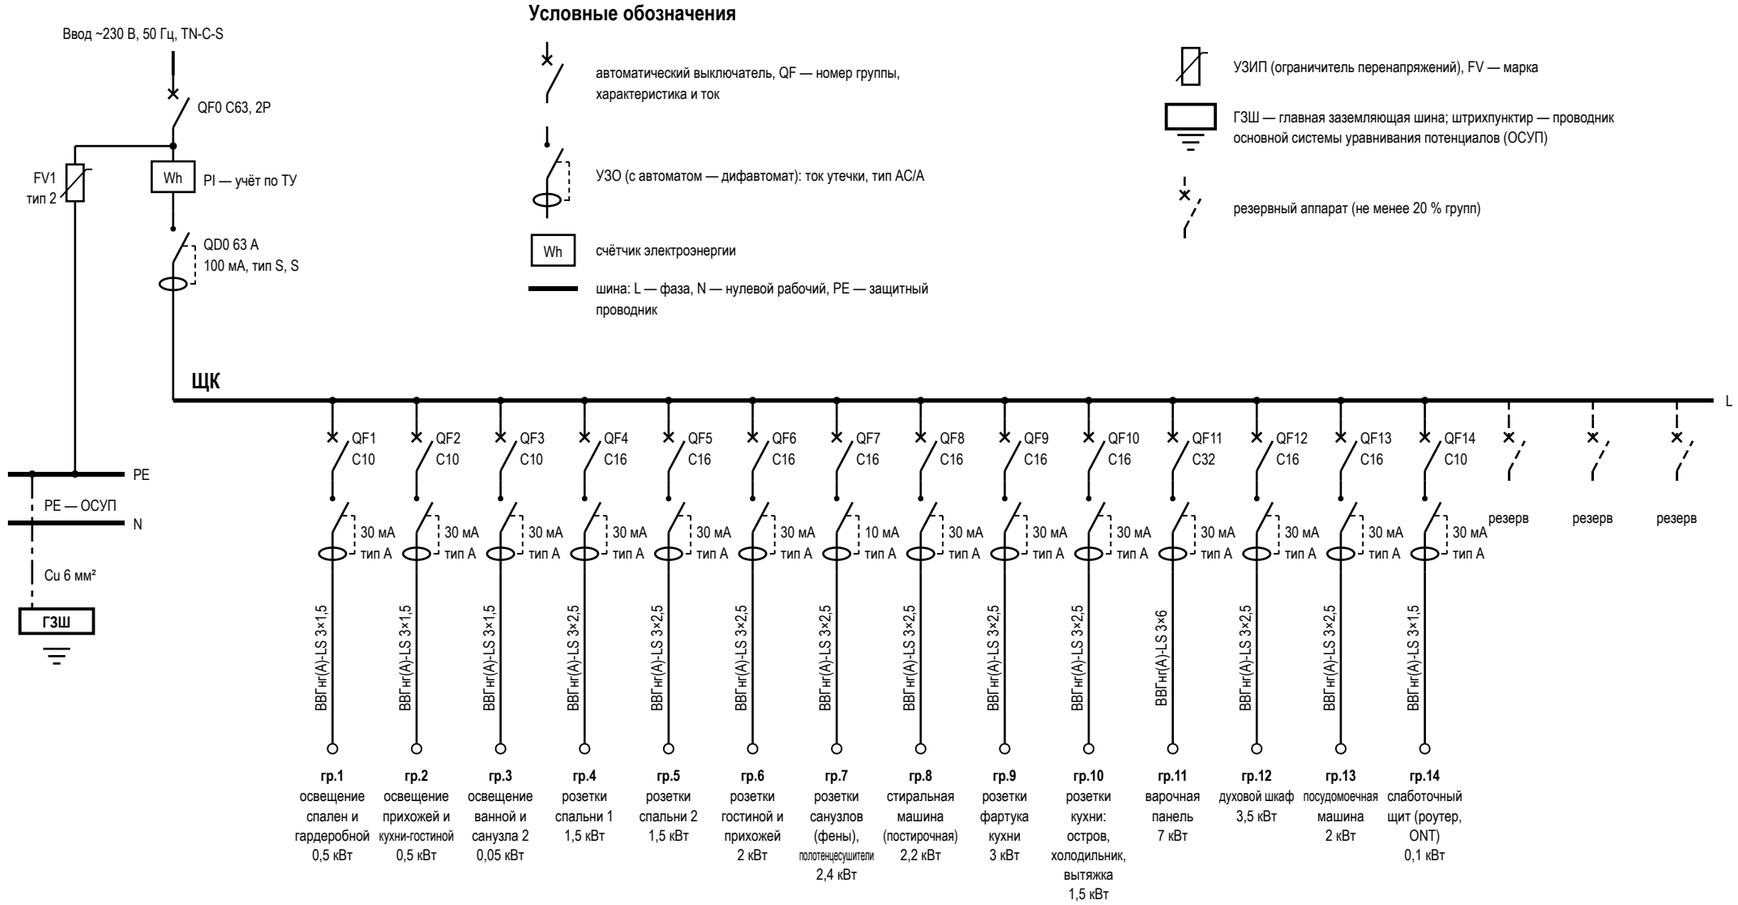

Данные щитка

Показатель	Значение
Номер щитка	ЩК
Тип	ЩРВ-П-24, IP41
Уст. мощность, кВт	27,75
Разреш. мощность, кВт	15
Расчётная, кВт	9,8
Автоматы 1п: занят. / рез.	14 / 3
Модулей: всего / занято	24 / 20
Ток на вводе, А	63
Вводной аппарат	QF0 C63, 2P
УЗИП	FV1, тип 2, ЩК, после счётчика
ГЗШ, проводник ОСУП	Cu 6 мм²

Таблица групп щита ЩК и кабельный журнал

№	Назначение	Помещения	Автомат	УЗО / дифавтомат	Кабель	Длина, м	P, кВт	Точек
1	освещение спален и гардеробной	1, 2, 3, 5, 7, 8, 10	C10	30 мА, тип A	ВВГнг(A)-LS 3×1,5	173,6	0,5	63
2	освещение прихожей и кухни-гостиной	4, 9	C10	30 мА, тип A	ВВГнг(A)-LS 3×1,5	41	0,5	11
3	освещение ванной и санузла 2	4, 6, 10, 11	C10	30 мА, тип A	ВВГнг(A)-LS 3×1,5	53,3	0,05	11
4	розетки спальни 1	10	C16	30 мА, тип A	ВВГнг(A)-LS 3×2,5	33	1,5	4
5	розетки спальни 2	1, 3, 8	C16	30 мА, тип A	ВВГнг(A)-LS 3×2,5	75,2	1,5	15
6	розетки гостиной и прихожей	4, 9	C16	30 мА, тип A	ВВГнг(A)-LS 3×2,5	26,2	2	3
7	розетки санузлов (фены), полотенцесушители	6, 11	C16	10 мА, тип A	ВВГнг(A)-LS 3×2,5	30	2,4	4
8	стиральная машина (постирочная)	7	C16	30 мА, тип A	ВВГнг(A)-LS 3×2,5	20	2,2	1
9	розетки фартука кухни	5	C16	30 мА, тип A	ВВГнг(A)-LS 3×2,5	16,6	3	2
10	розетки кухни: остров, холодильник, вытяжка	5	C16	30 мА, тип A	ВВГнг(A)-LS 3×2,5	19	1,5	4
11	варочная панель	5	C32	30 мА, тип A	ВВГнг(A)-LS 3×6	15,8	7	1
12	духовой шкаф	5	C16	30 мА, тип A	ВВГнг(A)-LS 3×2,5	35,3	3,5	1
13	посудомоечная машина	5	C16	30 мА, тип A	ВВГнг(A)-LS 3×2,5	53	2	1
14	слаботочный щит (роутер, ONT)	4	C10	30 мА, тип A	ВВГнг(A)-LS 3×1,5	3,5	0,1	1
	Итого по сечениям ВВГнг(A)-LS, м: 3×1,5 — 271,4; 3×2,5 — 308,3; 3×6 — 15,8					595,5		

Примечания

1. Схема однолинейная: одна линия — фаза, N и PE группы; аппараты — в отключённом положении (ГОСТ 2.702, ГОСТ 2.755). Номера групп — как у точек на планах (гр.). За отметку 0,000 принят уровень чистого пола; высота щита — по плану розеток.
2. Розеточные и мокрые линии — через УЗО или дифавтомат с током утечки не более 30 мА (ПУЭ 7.1.79); в санузле выполнить ДСУП (ПУЭ 7.1.87–7.1.88).
3. УЗО тип A — для линий с электроникой, стиральной и посудомоечной машиной, LED-драйверами; тип AC — только для чисто активной нагрузки.
4. Кабель — медный, исполнение нг(A)-LS (ГОСТ 31565-2012); скрытая прокладка только горизонтально и вертикально, фактические трассы зафиксировать исполнительной схемой до закрытия отделкой.
5. Номинал автомата — не выше допустимого тока кабеля: 1,5 мм² — до 10 А, 2,5 мм² — до 16 А. Резерв щита — не менее 20 % модулей.
6. Расчёт нагрузок, токов КЗ, селективности и сечений — по проекту ЭОМ организации с допуском СРО; лист задаёт состав, расположение и группы.
7. УЗИП FV1 — после вводного автомата, проводник к шине PE — кратчайший, без петель. Шина PE щита соединяется с ГЗШ проводником ОСУП; к ГЗШ присоединяются трубы водопровода и отопления на вводе в квартиру (ПУЭ 7.1.87). Шины N и PE — раздельные, после разделения PEN не объединяются.
8. До подключения нагрузки — приёмо-сдаточные испытания с протоколом: сопротивление изоляции линий не менее 0,5 МОм, срабатывание УЗО по току и времени, непрерывность защитных проводников PE (ПУЭ, гл. 1.8).

	Лист	№ док.	Подпись	Дата	Проект: Квартира 103 м²			
Дизайнер	Кырлан А.С.			14.11.26	Однолинейная схема щита	Стадия	Лист	Листов
Проверил						П	56	129
Н. контр.								
Утв.								

выпуск 14.11.2026 № 32d0256903 · стр. 56 из 129

Группы щита ЩК (1)

№	Назначение	Руст, кВт	Кс	Ррасч, кВт	Iрасч, А	Автомат	Кабель
1	освещение спален и гардеробной	0,5	0,6	0,3	1,4	C10	3×1,5
2	освещение прихожей и кухни-гостиной	0,5	0,6	0,3	1,4	C10	3×1,5
3	освещение ванной и санузла 2	0,05	0,6	0,03	0,1	C10	3×1,5
4	розетки спальни 1	1,5	0,4	0,6	2,7	C16	3×2,5
5	розетки спальни 2	1,5	0,4	0,6	2,7	C16	3×2,5
6	розетки гостиной и прихожей	2	0,4	0,8	3,7	C16	3×2,5
7	розетки санузлов (фены), полотенцесушители	2,4	0,7	1,68	7,7	C16	3×2,5

Группы щита ЩК (2)

№	Назначение	Руст, кВт	Кс	Ррасч, кВт	Iрасч, А	Автомат	Кабель
8	стиральная машина (постирочная)	2,2	0,7	1,54	7	C16	3×2,5
9	розетки фартука кухни	3	0,4	1,2	5,5	C16	3×2,5
10	розетки кухни: остров, холодильник, вытяжка	1,5	0,4	0,6	2,7	C16	3×2,5
11	варочная панель	7	0,6	4,2	19,2	C32	3×6
12	духовой шкаф	3,5	0,6	2,1	9,6	C16	3×2,5
13	посудомоечная машина	2	0,7	1,4	6,4	C16	3×2,5
14	слаботочный щит (роутер, ONT)	0,1	0,4	0,04	0,2	C10	3×1,5

Итог по квартире

Показатель	Значение
Установленная мощность Σ Руст	27,75 кВт
Σ Руст × Кс по группам	15,39 кВт
Коэффициент одновременности	0,7
Расчётная мощность квартиры Ррасч	10,8 кВт
Расчётный ток Iрасч (230 В, cosφ 0,95)	49 А
Разрешённая мощность	15 кВт
Запас до разрешённой	28,2 %
Вводной аппарат	C63, 2P


Примечания

1. Руст — установленная мощность группы по данным щита (приборы — по паспорту, розетки общего назначения — оценка 0,1 кВт на гнездо). Кс — коэффициенты спроса: освещение 0,6; розетки 0,4; варочная и духовой 0,6; кондиционеры 0,8; тёплый пол 1,0; прочие 0,7; одновременность 0,7.
2. Коэффициенты — ориентир исполнителя, не табличные значения нормы; расчёт нагрузки подтверждает инженер ЭОМ (СП 256.1325800.2016). Под разрешённую мощность они не подгоняются.
3. Вывод: запас 28 % (расчётная 10,8 кВт при разрешённой 15 кВт).
4. Розеточные и мокрые линии — через УЗО или дифавтомат с током утечки не более 30 мА (ПУЭ 7.1.79); в санузле выполнить ДСУП (ПУЭ 7.1.87–7.1.88).

выпуск 14.11.2026 № 32d0256903 · стр. 57 из 129

	Лист	№ док.	Подпись	Дата	Проект: Квартира 103 м²			
Дизайнер	Кырлан А.С.			14.11.26	Таблица нагрузок щита	Стадия	Лист	Листов
Проверил						П	57	129
Н. контр.								
Утв.								

План принципиальных трасс (М 1:75)

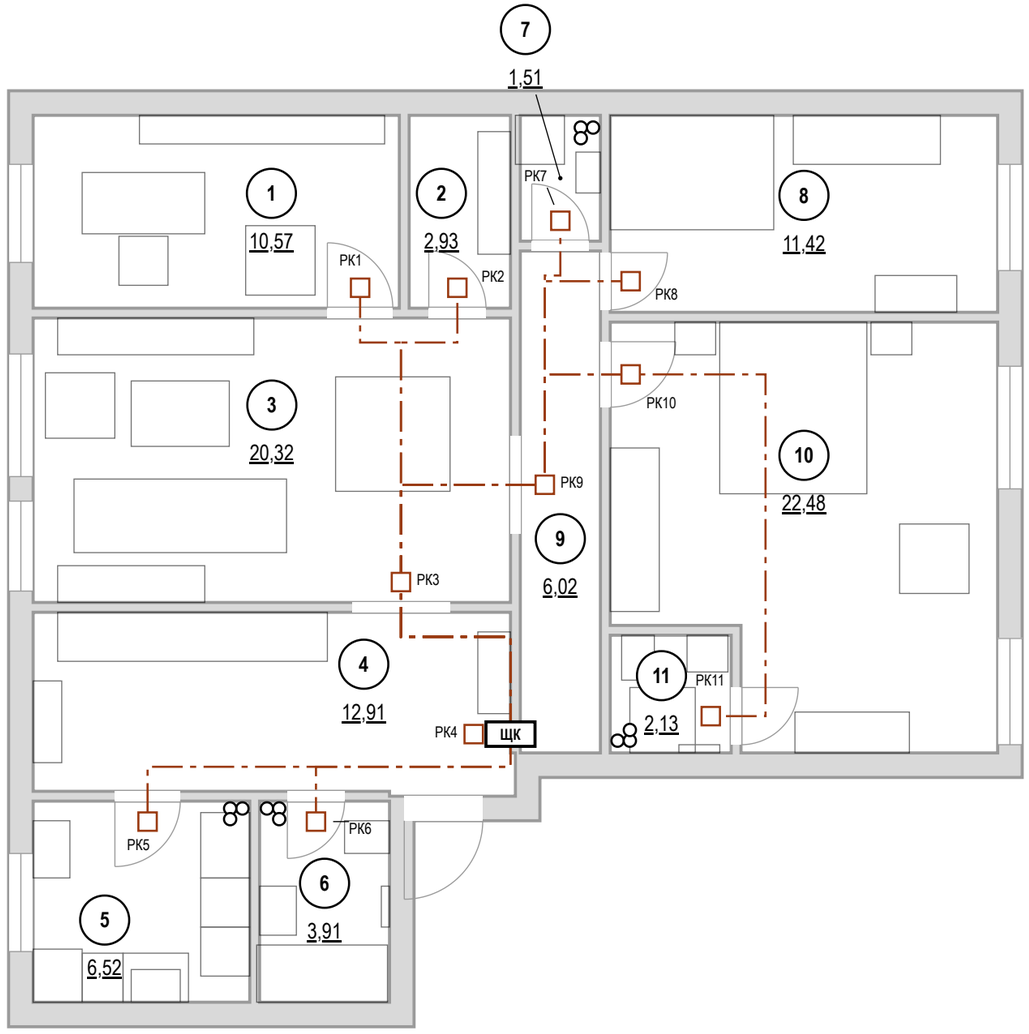

Кабель по группам ВВГнг(А)-LS, м

Гр.	мм²	Трасса	Данные
1	3×1,5	175,3	173,6
2	3×1,5	40,9	41
3	3×1,5	55,1	53,3
4	3×2,5	33	33
5	3×2,5	75,2	75,2
6	3×2,5	26,2	26,2
7	3×2,5	41,2	30

Гр.	мм²	Трасса	Данные
8	3×2,5	17,9	20
9	3×2,5	16,6	16,6
10	3×2,5	19	19
11	3×6	15,8	15,8
12	3×2,5	15,4	35,3
13	3×2,5	13,4	53
14	3×1,5	3,5	3,5
Σ		**548,5**	**595,5**

Экспликация помещений

№	Помещение	Площадь, м²
1	Кабинет-библиотека	10,57
2	Кладовая	2,93
3	Гостиная-столовая	20,32
4	Прихожая-холл	12,91
5	Кухня	6,52
6	Ванная	3,91
7	Постирочная	1,51
8	Спальня 2	11,42
9	Коридор	6,02
10	Спальня мастер	22,48
11	Ванная мастер	2,13
	Итого (общая площадь)	100,72

Объёмы прокладки

Работа, материал	Ед.	Кол.
Гофротруба Ø20 в потолочном пространстве	м	251,6
Кабель-канал плинтуса для силовых линий	м	130,1
Короб или накладной канал для вертикальных спусков и подъёмов	м	83,8
Коробка распределительная (РК) над дверью помещения	шт	11
Слаботочка: кабель домофона	м	4,3
Слаботочка: Кабель коаксиальный RG-6 (75 Ом) к розеткам ТВ	м	16,1
Слаботочка: U/UTP кат. 6 (LAN, Wi-Fi, камеры)	м	70,3
Слаботочка: гофротруба Ø20 отдельно от силовых	м	81,6

Штробы — только после заключения

Работа	Ед.	Кол.
Вертикальные штробы 20×20 мм от потолка до каждой настенной точки (в маршрут без штроб не входят)	м	103,59

Условные обозначения

- **ЩК** — щит квартирный
- РК — распределительная коробка над дверью помещения
- магистраль от щита к РК: потолочное пространство, гофра
- мебель и сантехприборы — подложка


Примечания

1. За отметку 0,000 принят уровень чистого пола. Высоты Н — от чистого пола до оси изделия; привязки — от чистовой грани стены до оси механизма (у рамки на несколько постов — до оси рамки).
2. Розеточные и мокрые линии — через УЗО или дифавтомат с током утечки не более 30 мА (ПУЭ 7.1.79); в санузле выполнить ДСУП (ПУЭ 7.1.87–7.1.88).
3. Кабель — медный, исполнение нг(А)-LS (ГОСТ 31565-2012); скрытая прокладка только горизонтально и вертикально, фактические трассы зафиксировать исполнительной схемой до закрытия отделкой.
4. Расчёт нагрузок, токов КЗ, селективности и сечений — по проекту ЭОМ организации с допуском СРО; лист задаёт состав, расположение и группы.
5. Длины — по плану: от щита вверх в потолочное пространство, по дверям и коридору без захода в мокрые помещения к распределительной коробке над дверью, далее к точкам; вертикали считаются вниз и обратно (у последней точки цепочки — в один конец); запас 10 %. Трассы принципиальные: фактическую зафиксировать исполнительной схемой до закрытия отделкой.
6. Несущие стены не определены: штробы в стенах не выполнять. Маршрут проложен без штроб: горизонтали — за потолком в гофре (251,6 м) и в кабель-канале плинтуса (130,1 м), вертикали — в коробе или накладном канале (147,4 м кабеля). Точек: за потолком — 59, спуск из потолка — 13, по плинтусу — 19, плинтус и подъём 31.
7. Вариант со штробами — работа после технического заключения: 103,59 м вертикальных штроб от потолка до каждой настенной точки; условие — только после технического заключения: стена не несущая (или вертикальная штроба в несущей согласована конструктором), глубина и ширина 20–25 мм, не в зонах 0–2 ванной. Без заключения и согласования конструктора в смету и в график эта работа не входит.
8. В данных проекта (журнал щита) длины кабеля внесены оценкой (596 м), по трассам из геометрии — 549 м (-8 %): к закупке и в смету принимать длины по трассам, а оценку в данных проекта заменить.
9. Слаботочные сети: кабели и точки считаются по лучам от ЩС (лист слаботочных сетей): 91 м, портов патч-панели и коммутатора не менее 5; из точек 2 предложения листа слаботочки, не подтверждённые заказчиком. Изделия — в ведомости изделий.

	Лист	№ док.	Подпись	Дата	Проект: Квартира 103 м²			М 1:75
Дизайнер	Кырлан А.С.			14.11.26	План принципиальных трасс	Стадия	Лист	Листов
Проверил						П	58	129
Н. контр.								
Утв.								

выпуск 14.11.2026 № 32d0256903 · стр. 58 из 129

План розеток (М 1:50)

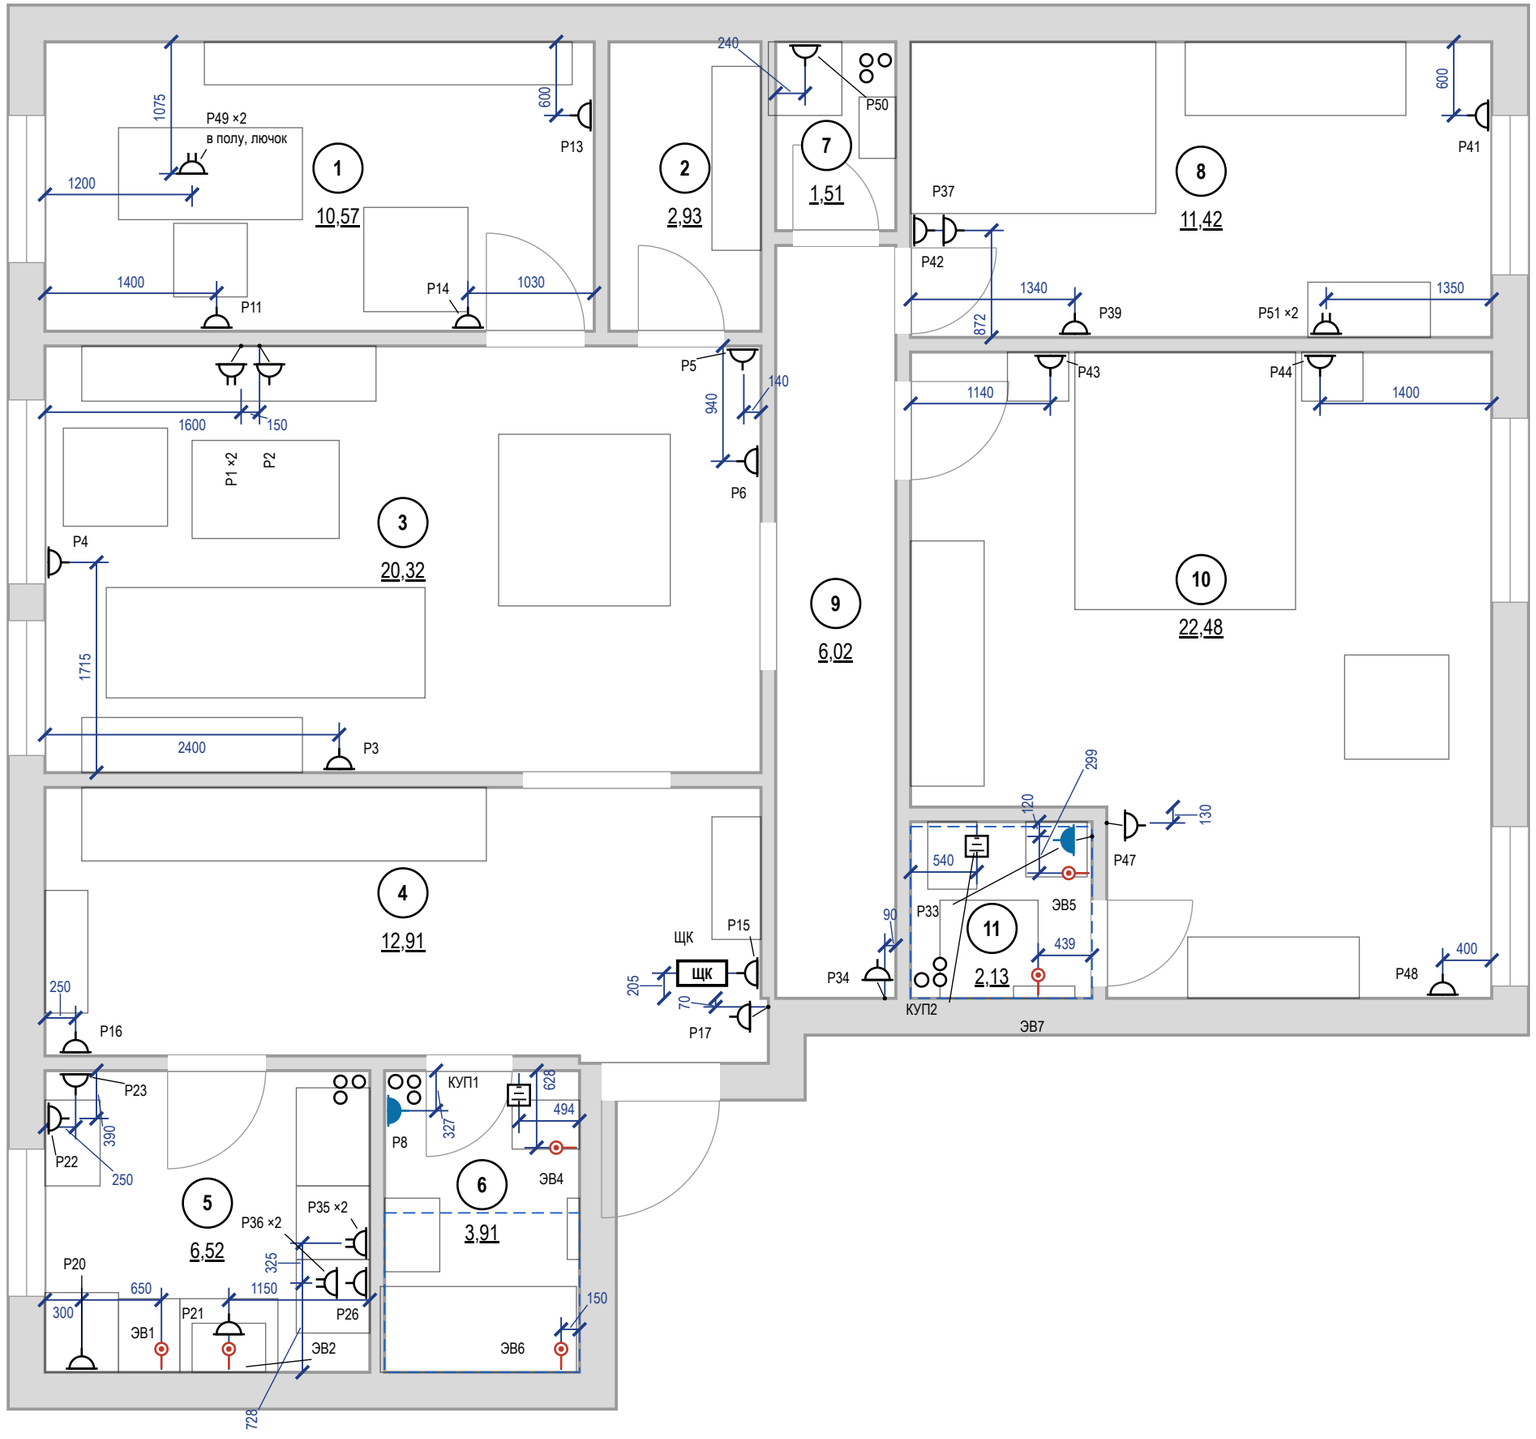

Условные обозначения

Знак	Тип изделия	H, мм	Кол., шт
	Розетка с заземлением	300	17
	То же	у знака	9
	Блок розеток с заземлением, рамка 2 поста	у знака	5
	Розетка с заземлением IP44	1000	2
	Вывод кабеля к прибору	у знака	6
	КУП (уравнивание потенциалов)	300	2
ЩК	Щит квартирный	1700	1

розетка с заземляющим контактом; у знака — марка и ×N — число постов в рамке; группа щита, высота оси и назначение — в ведомости точек

знак разведён для читаемости: точка на стене — у выноски, привязка — до неё

граница зоны 2 ванной (600 мм от ванны/поддона)

мебель и сантехприборы — подложка

стояк: К1 — канализация, В1 — ХВС, Т3 — ГВС

1 — номер помещения, площадь м²

Итого розеток (механизмов) — 38 шт; рамок — 33 шт: на 1 пост — 28, на 2 поста — 5.


Примечания

1. За отметку 0,000 принят уровень чистого пола. Высоты H — от чистого пола до оси изделия; привязки — от чистовой грани стены до оси механизма (у рамки на несколько постов — до оси рамки).
2. Высоты H и группы щита — в ведомости электроточек: розетки — 300 мм от чистого пола до оси механизма, если в ведомости не указано иное; выводы кабеля — по паспорту прибора.
3. Розетки в санузле — только вне зон 0–2 (ПУЭ 7.1.48, ГОСТ Р 50571.7.701-2024), IP44, через УЗО 30 мА.
4. Розеточные и мокрые линии — через УЗО или дифавтомат с током утечки не более 30 мА (ПУЭ 7.1.79); в санузле выполнить ДСУП (ПУЭ 7.1.87–7.1.88).
5. Кабель — медный, исполнение нг(А)-LS (ГОСТ 31565-2012); скрытая прокладка только горизонтально и вертикально, фактические трассы зафиксировать исполнительной схемой до закрытия отделкой.
6. Расчёт нагрузок, токов КЗ, селективности и сечений — по проекту ЭОМ организации с допуском СРО; лист задаёт состав, расположение и группы.
7. Выводы кухонной техники — после утверждения проекта кухни (ориентировочно); привязки выводов даны от осей модулей гарнитура и пересматриваются вместе с проектом кухни.
8. Электрический тёплый пол проектом не предусмотрен; при решении заказчика устроить — отдельный лист «План тёплых полов»: контуры с отступом 100 мм от стен и мебели без ножек, датчик в гофре, терморегулятор, своя группа щита через УЗО 30 мА.

	Лист	№ док.	Подпись	Дата	Проект: Квартира 103 м²			М 1:50
Дизайнер	Кырлан А.С.			14.11.26	План розеток и электровыводов	Стадия	Лист	Листов
Проверил						П	59	129
Н. контр.								
Утв.								

выпуск 14.11.2026 № 32d0256903 · стр. 59 из 129

План слаботочных сетей (М 1:50)

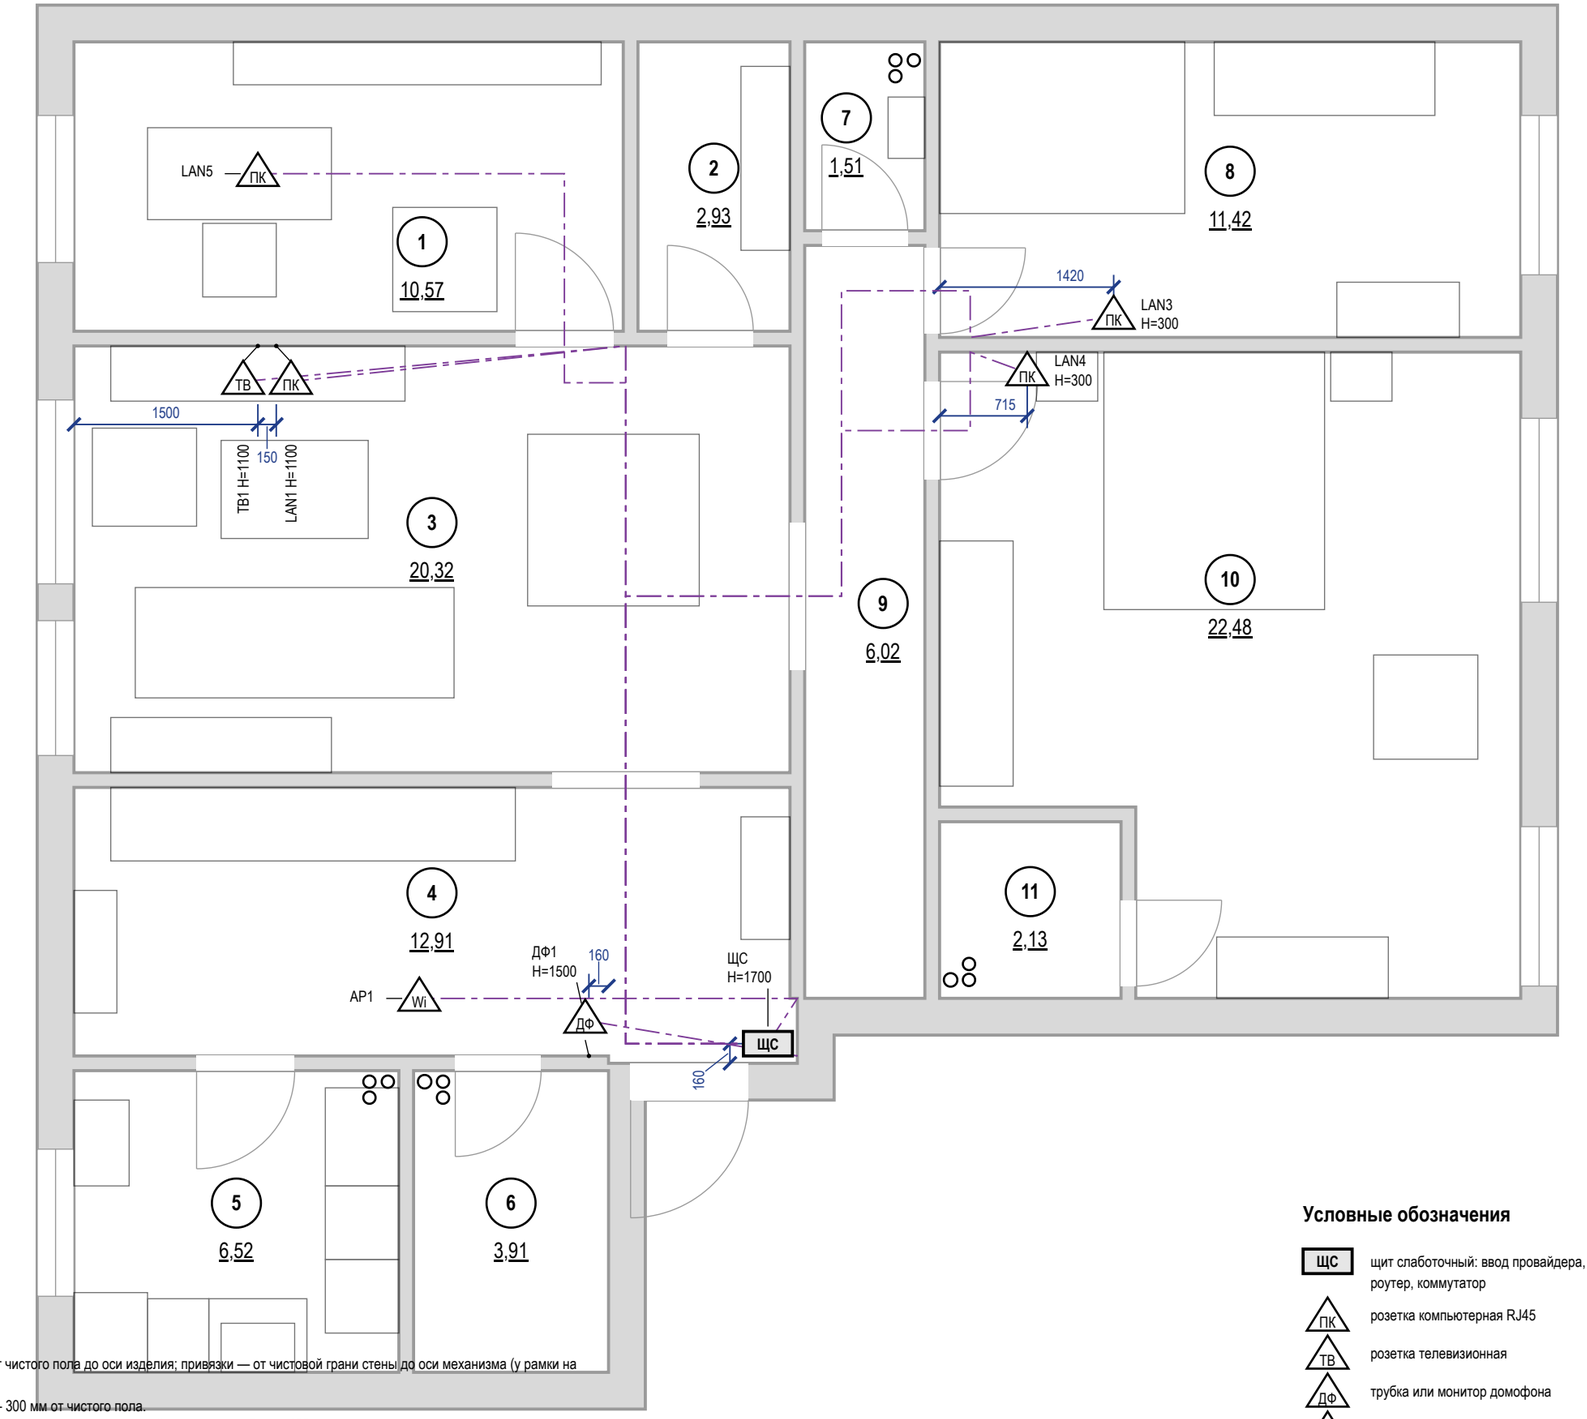

Условные обозначения

- ЩС — щит слаботочный: ввод провайдера, роутер, коммутатор
- ПК — розетка компьютерная RJ45
- ТВ — розетка телевизионная
- ДФ — трубка или монитор домофона
- Wi — точка доступа Wi-Fi (питание PoE)
- кабель от ЩС до точки, отдельным лучом
- мебель и сантехприборы — подложка
- стояк: К1 — канализация, В1 — ХВС, Т3 — ГВС
- 1 — номер помещения, площадь м²


Примечания

1. За отметку 0,000 принят уровень чистого пола. Высоты Н — от чистого пола до оси изделия; привязки — от чистовой грани стены до оси механизма (у рамки на несколько постов — до оси рамки).
2. Высота установки, не указанная на плане: розетки LAN и ТВ — 300 мм от чистого пола.
3. Слаботочные кабели — отдельно от силовых: в своей трубе или лотке, при параллельной прокладке не ближе 100 мм к силовым, пересечения под прямым углом; каждую точку — отдельным кабелем от ЩС без скруток.
4. Трассы на листе — принципиальные; фактические зафиксировать исполнительной схемой до закрытия отделкой. Силовые линии, УЗО 30 мА, ДСУП, кабель нг(A)-LS — по листам розеток и щита.
5. Проект силовой части и расчёт токов КЗ — по проекту ЭОМ; слаботочная часть согласуется с провайдером и управляющей компанией (домофон, коллективное ТВ).

	Лист	№ док.	Подпись	Дата	Проект: Квартира 103 м²			М 1:50
Дизайнер	Кырлан А.С.			14.11.26	План слаботочных сетей	Стадия	Лист	Листов
Проверил						П	60	129
Н. контр.								
Утв.								

выпуск 14.11.2026 № 32d0256903 · стр. 60 из 129

План освещения (М 1:50)

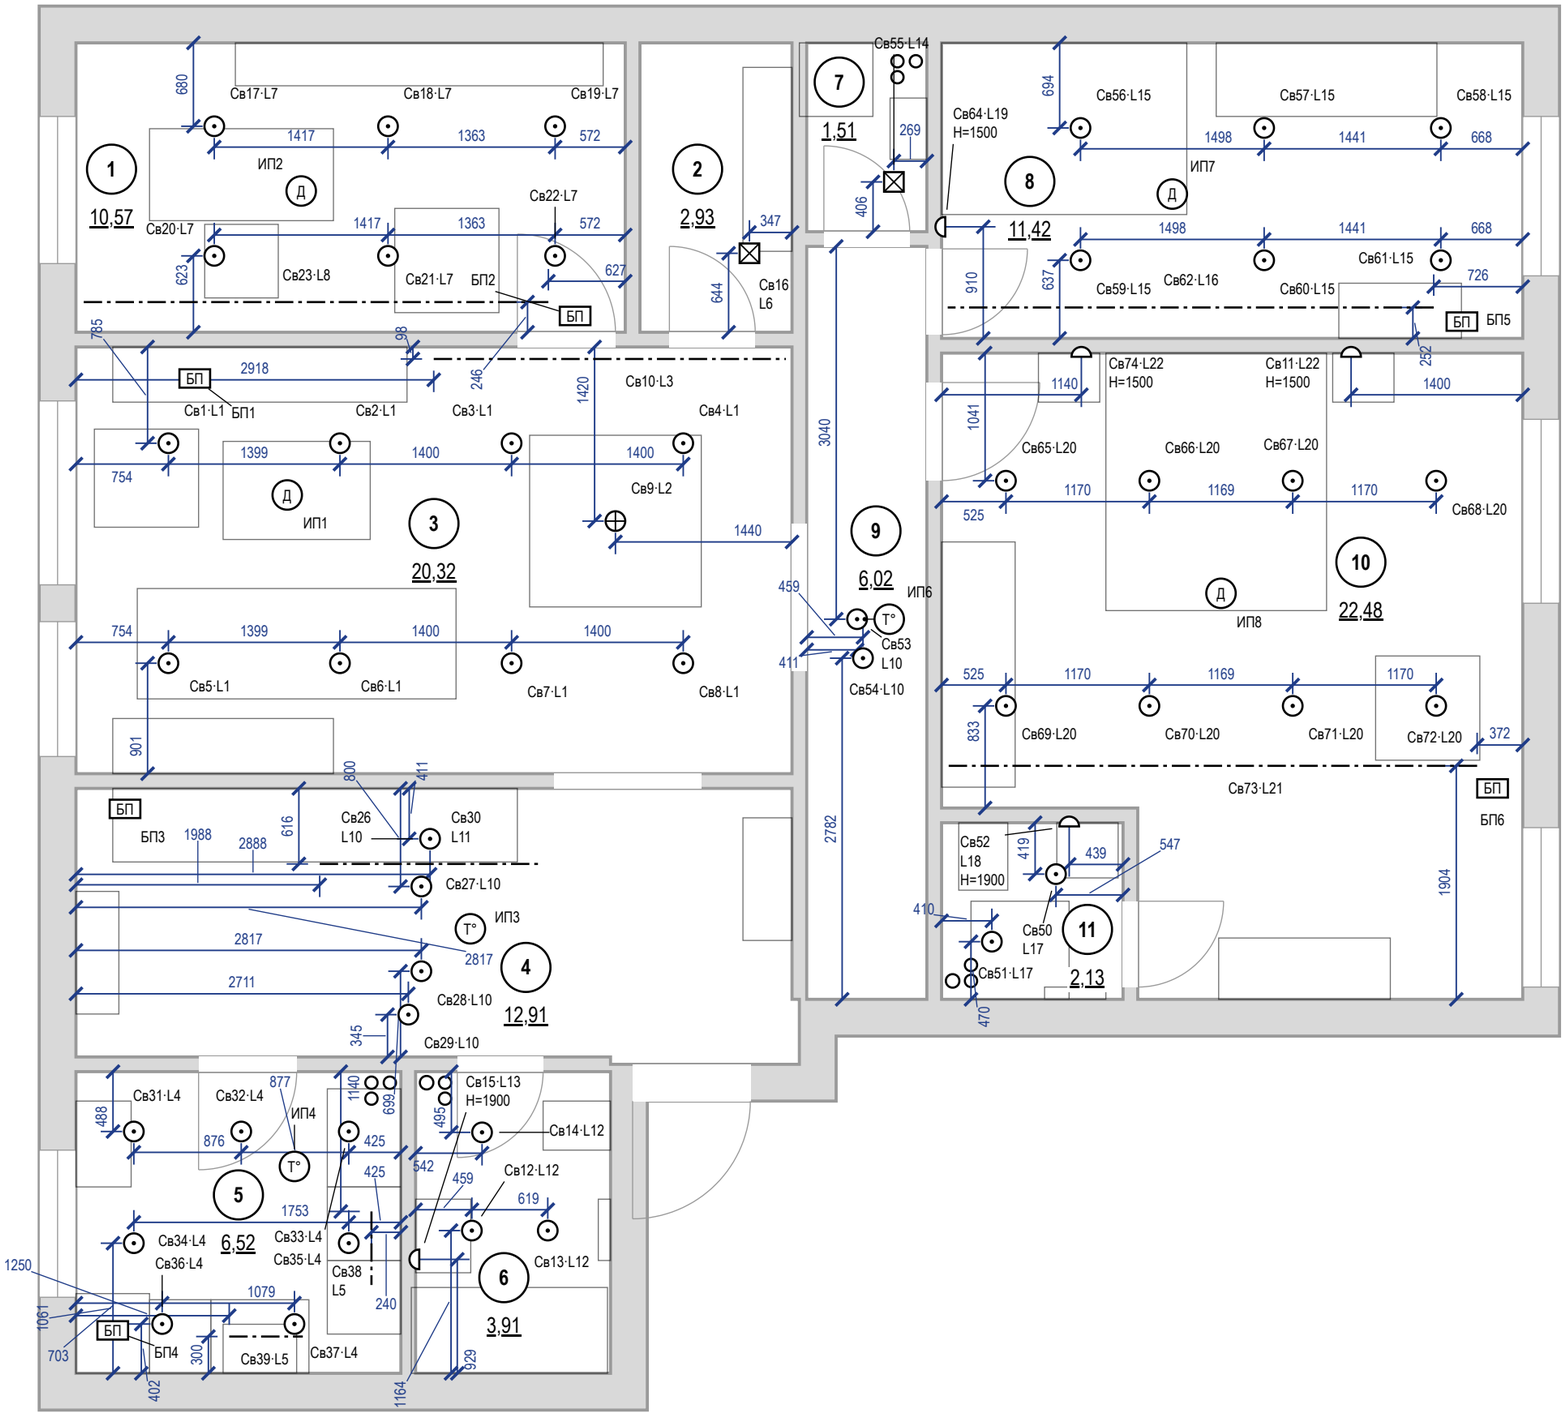

Условные обозначения

- светильник встраиваемый точечный
- светильник потолочный накладной
- светильник подвесной
- светильник настенный (бра), Н — высота оси
- светодиодная лента в профиле / в карнизе короба
- Св1·L1 — марка светильника (как в ведомости и на развёртках) · группа включения L (лист 63)
- Д — извещатель пожарный дымовой автономный
- Т° — извещатель пожарный тепловой
- БП — блок питания LED, с доступом (люк от 100×100 мм)
- мебель и сантехприборы — подложка
- стояк: К1 — канализация, В1 — ХВС, Т3 — ГВС
- 1 — номер помещения, площадь м²

Примечания

1. За отметку 0,000 принят уровень чистого пола. Высоты Н — от чистого пола до оси изделия; привязки — от чистовой грани стены до оси механизма (у рамки на несколько постов — до оси рамки).
2. Высота установки, не указанная на плане: светильники — на потолке; настенные — по отметке Н у знака. Привязки — до оси светильника от чистовой грани стены, по рядам.
3. Во влажных помещениях — светильники не ниже IP44; в зонах 0–2 ванной — по ГОСТ Р 50571.7.701-2024 (зона 1 — IPX5).
4. Розеточные и мокрые линии — через УЗО или дифавтомат с током утечки не более 30 мА (ПУЭ 7.1.79); в санузле выполнить ДСУП (ПУЭ 7.1.87–7.1.88).
5. Кабель — медный, исполнение нг(А)-LS (ГОСТ 31565-2012); скрытая прокладка только горизонтально и вертикально, фактические трассы зафиксировать исполнительной схемой до закрытия отделок.
6. Расчёт нагрузок, токов КЗ, селективности и сечений — по проекту ЭОМ организации с допуском СРО; лист задаёт состав, расположение и группы.
7. Ведомость светильников (тип, количество, мощность, поток, Тц, Ra) — лист 62.

	Лист	№ док.	Подпись	Дата
Дизайнер	Кырлан А.С.			14.11.26
Проверил				
Н. контр.				
Утв.				

Проект: Квартира 103 м² — **М 1:50**

План освещения

Стадия	Лист	Листов
П	61	129

выпуск 14.11.2026 № 32d0256903 · стр. 61 из 129

Параметры светильников для подбора

Поз.	Марки	Наименование	Установка	Кол.	P, Вт	Σ P, Вт	Ф, лм	Тц, К	Ra	Угол, °	IP	Дим.	Слой	Группа	Пом.
1	Св17–Св22, Св56–Св61	Встраиваемый точечный	в ГКЛ, корпус ≤ 70 мм	12	12	144	1050	2700	90	—	20	—	общий	L7, L15	1, 8
2	Св23, Св62	Лента светодиодная 24 В	на поверхности, профиль с рассеивателем	24,6 м	9,6/м	236,2	900/м	2700	90	—	20	да	акцентный	L8, L16	1, 8
3	Св16, Св55	Потолочный накладной	на потолке, засветка стены	2	10	20	900	3000	90	—	20	—	общий	L6, L14	2, 7
4	Св1–Св8, Св31–Св37	Встраиваемый точечный	в ГКЛ, корпус ≤ 70 мм	15	12	180	1000	3000	90	—	20	—	общий	L1, L4	3, 5
5	Св9	Подвесной	подвес, низ H=1600	1	15	15	1200	2700	90	—	20	—	рабочий	L2	3
6	Св10	Лента светодиодная 24 В	на поверхности, профиль с рассеивателем	5,4 м	9,6/м	51,8	900/м	2700	90	—	20	да	акцентный	L3	3
7	Св26–Св29, Св53, Св54	Встраиваемый точечный	в ГКЛ, корпус ≤ 70 мм	6	7	42	600	3000	90	—	20	—	общий	L10	4, 9
8	Св30	Лента светодиодная 24 В	на поверхности, профиль с рассеивателем, датчик движения	1,8 м	4,8/м	8,6	150/м	2700	90	—	20	нет	ночной	L11	4
9	Св38, Св39	Линейный светильник	на поверхности	1,2 м	8	16	700	3000	90	—	20	—	рабочий	L5	5
10	Св12–Св14, Св51	Встраиваемый точечный	в ГКЛ, корпус ≤ 70 мм	4	6	24	500	3000	90	—	44	—	общий	L12, L17	6, 11
11	Св15, Св52	Настенный светильник над зеркалом, драйвер встроен	над зеркалом, H=1900	2	8	16	600	3000	90	—	44	—	рабочий	L13, L18	6, 11
12	Св11, Св64, Св74	Настенный (бра)	на стене, H=1500	3	6	18	400	2700	90	60	20	—	рабочий	L19, L22	8, 10
13	Св65–Св72	Встраиваемый точечный	в ГКЛ, корпус ≤ 70 мм	8	12	96	1000	2700	90	—	20	—	общий	L20	10
14	Св73	Лента светодиодная 24 В	на поверхности, профиль с рассеивателем	15,5 м	9,6/м	148,8	900/м	2700	90	—	20	да	акцентный	L21	10
15	Св50	Встраиваемый точечный	в ГКЛ, корпус ≤ 70 мм	1	7	7	600	3000	90	—	44	—	общий	L17	11
		Итого		**54 шт + 48,5 м**		**1023,4**									

LED-ленты, линейные светильники и блоки питания

Марка	Пом.	L, м	U, В	Вт/м	Σ P, Вт	БП	P БП, Вт	Загр., %	Питание	Доступ к БП
Св23	1	12,3	24	9,6	118,1	БП2	200	59	с двух концов	люк 300×300 в коробе У1 у окна
Св10	3	5,4	24	9,6	51,8	БП1	100	52	с одного конца	люк 300×300 в коробе потолка у стены А
Св30	4	1,8	24	4,8	8,6	БП3	20	43	с одного конца	в шкафу М-11, верхняя полка
Св38	5	0,6	24	—	8	БП4	30	53	встроенный ввод	в колонне М-19 над холодильником, съёмная панель
Св39	5	0,6	24	—	8	БП4	30	53	встроенный ввод	в колонне М-19 над холодильником, съёмная панель
Св62	8	12,3	24	9,6	118,1	БП5	200	59	с двух концов	люк 300×300 в коробе У1 у окна
Св73	10	15,5	24	9,6	148,8	БП6	200	74	с двух концов	люк 300×300 в коробе У1 у входа

Сценарии (помещения со светорегуляторами)


Помещение	Сценарий	Горят группы (уровень)	Управление
3. Гостиная-столовая	Вечер	L2 подвес над обеденным столом — вкл.; L3 лента в карнизе (диммер) — 50 %; остальные выкл.	светорегулятор S2; выключатель S1
	Гости	L1 общий свет (споты) — вкл.; L2 подвес над обеденным столом — вкл.; L3 лента в карнизе (диммер) — 100 %	светорегулятор S2; выключатель S1
	Кино	L3 лента в карнизе (диммер) — 20 %; остальные выкл.	светорегулятор S2
	Уборка	L1 общий свет (споты) — вкл.; L2 подвес над обеденным столом — вкл.; остальные выкл.	выключатель S1

Примечания

1. Позиции и марки Св — те же, что на плане освещения (лист 61); группы L — по плану выключателей (лист 63).
2. Модели светильников не выбраны: лист — техническое задание на подбор. Модель по строке таблицы: поток, Тц, Ra, угол, IP и регулировка яркости не хуже указанных, мощность не больше; встраиваемые — под глубину короба (графа «Установка»). IP 20 — сухие помещения. После выбора моделей (артикул, производитель) лист выпускается как «Спецификация светильников».
3. Длина LED-ленты в карнизе — по линии карниза плана потолков (лист 52); Σ P = Вт/м × длина. Блок питания загружен не больше чем на 80 %; лента 24 В длиннее 10 м питается с двух концов; доступ к блоку питания — люк ревизии 300×300 мм или место, указанное в таблице.
4. Сценарии: % — яркость группы на светорегуляторе; «вкл.» — группа на обычной клавише; группы, не названные в строке, выключены. Светильники и блоки питания групп на светорегуляторе — с регулировкой яркости. Клавиши и светорегуляторы — лист 63.
5. В пом. 1, 8, 10 свет включается клавишами групп — лист 63.
6. Мощность и поток в таблице — требования к подбору (поток не меньше, мощность не больше указанных); после выбора модели — по её паспорту, Σ P — установленная мощность освещения. Оценка освещённости — на плане освещения; это не светотехнический расчёт.

	Лист	№ док.	Подпись	Дата	Проект: Квартира 103 м²			
Дизайнер	Кырлан А.С.			14.11.26	Техническое задание на подбор светильников	Стадия	Лист	Листов
Проверил						П	62	129
Н. контр.								
Утв.								

План выключателей (М 1:50)

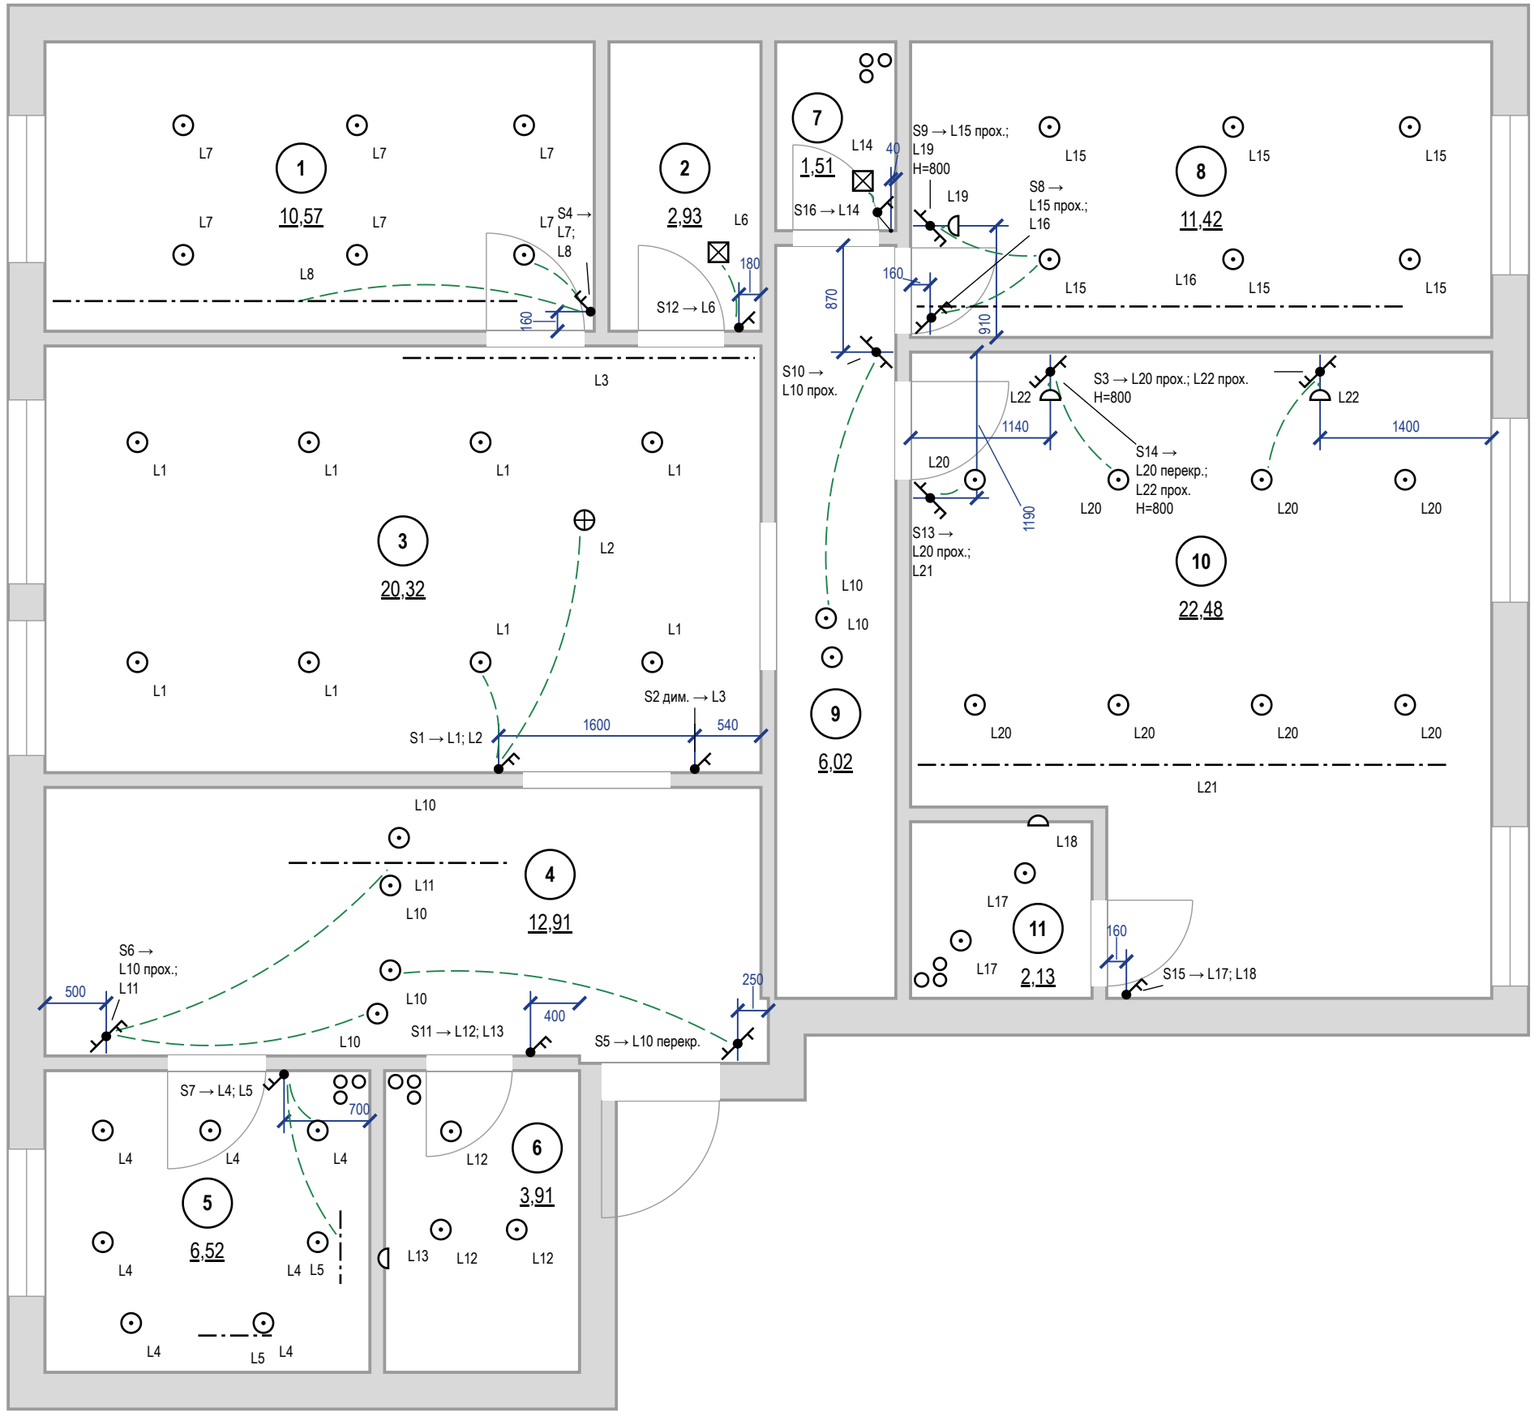

Условные обозначения

- выключатель одноклавишный
- выключатель двухклавишный (флажков — по числу клавиш)
- выключатель с проходной или перекрёстной клавишей (обратный флажок); тип клавиши — в подписи
- S1 → — марка → группы по клавишам (через «;»): прох. — проходной, перекр. — перекрёстный, дим. — светорегулятор; H — высота
- связь: выключатель → ближайший светильник группы в том же помещении (не трасса кабеля); полный состав группы — по номеру L
- светильник встраиваемый точечный
- светильник потолочный накладной
- светильник подвесной
- светильник настенный (бра), H — высота оси
- светодиодная лента в профиле / в карнизе короба
- L1 — группа включения у светильника
- стояк: К1 — канализация, В1 — ХВС, Т3 — ГВС
- 1 — номер помещения, площадь м²


Примечания

1. За отметку 0,000 принят уровень чистого пола. Высоты H — от чистого пола до оси изделия; привязки — от чистовой грани стены до оси механизма (у рамки на несколько постов — до оси рамки).
2. Высота установки, не указанная на плане: выключатели — 900 мм от чистого пола (у кровати и другие — H у марки), со стороны дверной ручки (ПУЭ 7.1.51).
3. Какой выключатель какие светильники включает — по номеру группы L: у выключателя (S1 → L1; L2 — клавиши по порядку) и у каждого светильника. Пунктир — подсказка к ближайшему светильнику группы в том же помещении (не дальше 3 м), это не трасса кабеля; выключатель за стеной (у двери санузла) и далёкая группа только номер группы.
4. Группы из нескольких мест (L10 — S5, S6, S10; L15 — S8, S9; L20 — S3, S13, S14; L22 — S3, S14): на крайних местах — проходные клавиши, на промежуточных — перекрёстные; механизмы — в ведомости изделий.
5. Светорегулятор — по заднему фронту (для LED-драйверов), совместимость с драйверами проверить до закупки.
6. Розеточные и мокрые линии — через УЗО или дифавтомат с током утечки не более 30 мА (ПУЭ 7.1.79); в санузле выполнить ДСУП (ПУЭ 7.1.87–7.1.88).
7. Кабель — медный, исполнение нг(А)-LS (ГОСТ 31565-2012); скрытая прокладка только горизонтально и вертикально, фактические трассы зафиксировать исполнительной схемой до закрытия отделки.
8. Расчёт нагрузок, токов КЗ, селективности и сечений — по проекту ЭОМ организации с допуском СРО; лист задаёт состав, расположение и группы.

	Лист	№ док.	Подпись	Дата	Проект: Квартира 103 м²			М 1:50
Дизайнер	Кырлан А.С.			14.11.26	Управление светильниками	Стадия	Лист	Листов
Проверил						П	63	129
Н. контр.								
Утв.								

выпуск 14.11.2026 № 32d0256903 · стр. 63 из 129

План вентиляции (М 1:50)

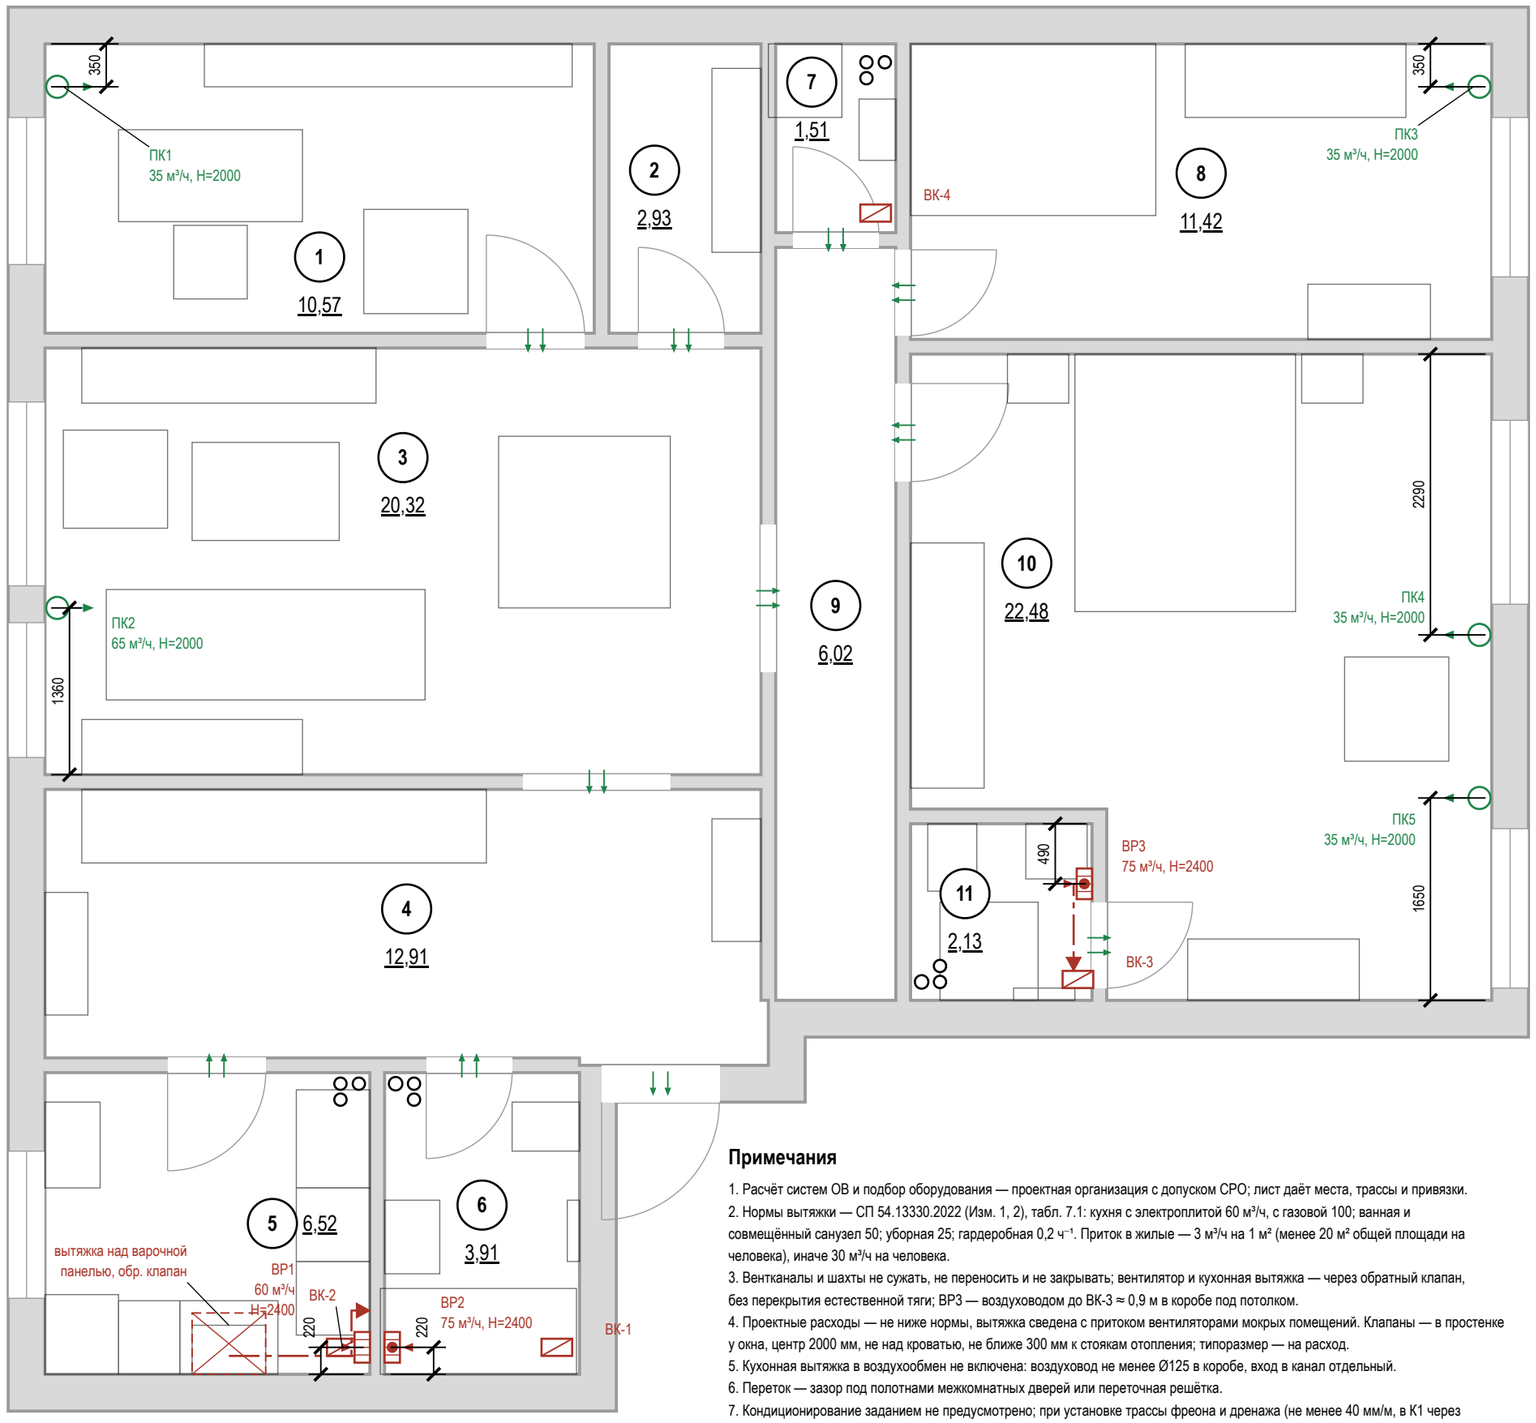

Условные обозначения

- стояк: К1 — канализация, В1 — ХВС, Т3 — ГВС
- номер помещения, площадь м²
- вытяжная решётка в вентканал: марка, расход м³/ч, Н центра от чистого пола
- вытяжная решётка с бытовым вентилятором и обратным клапаном: марка, расход, Н
- приточный клапан (КИВ) в наружной стене: марка, расход, Н центра
- переток: зазор под полотном или переточная решётка
- кухонная вытяжка над варочной панелью
- вентканал ВК-N в стене или вентблоке
- воздуховод в коробе под потолком (за подшивным потолком) до вентканала
- отдельный вход воздуховода в вентканал, обратный клапан

Воздухообмен, м³/ч

№	Помещение	Выт. норма	Выт. проект	Прит. норма	Прит. проект	Устрой-ства
1	Кабинет-библиотека			32	35	ПК1
2	Кладовая	2				переток
3	Гостиная-столовая			61	65	ПК2
5	Кухня	60	60			ВР1
6	Ванная	50	75			ВР2
7	Постирочная	1				переток
8	Спальня 2			35	35	ПК3
10	Спальня мастер			68	70	ПК4, ПК5
11	Ванная мастер	50	75			ВР3
	Итого	**163**	**210**	**196**	**205**	
	Норма по жильцам: 30×2			60		

Воздухообмен квартиры — по большей из сумм притока и вытяжки: норма 196 м³/ч, проект 210 м³/ч.
Вытяжка не меньше притока — баланс сведён.

Примечания

1. Расчёт систем ОВ и подбор оборудования — проектная организация с допуском СРО; лист даёт места, трассы и привязки.
2. Нормы вытяжки — СП 54.13330.2022 (Изм. 1, 2), табл. 7.1: кухня с электроплитой 60 м³/ч, с газовой 100; ванная и совмещённый санузел 50; уборная 25; гардеробная 0,2 ч⁻¹. Приток в жилые — 3 м³/ч на 1 м² (менее 20 м² общей площади на человека), иначе 30 м³/ч на человека.
3. Вентканалы и шахты не сужать, не переносить и не закрывать; вентилятор и кухонная вытяжка — через обратный клапан, без перекрытия естественной тяги; ВР3 — воздуховодом до ВК-3 ≈ 0,9 м в коробе под потолком.
4. Проектные расходы — не ниже нормы, вытяжка сведена с притоком вентиляторами мокрых помещений. Клапаны — в простенке у окна, центр 2000 мм, не над кроватью, не ближе 300 мм к стоякам отопления; типоразмер — на расход.
5. Кухонная вытяжка в воздухообмен не включена: воздуховод не менее Ø125 в коробе, вход в канал отдельный.
6. Переток — зазор под полотнами межкомнатных дверей или переточная решётка.
7. Кондиционирование заданием не предусмотрено; при установке трассы фреона и дренажа (не менее 40 мм/м, в К1 через сифон) и питание заложить до черновых работ.
8. Привязки оборудования — по паспортам приобретённых моделей, до черновых работ.

	Лист	№ док.	Подпись	Дата
Дизайнер	Кырлан А.С.			14.11.26
Проверил				
Н. контр.				
Утв.				


Проект: Квартира 103 м² — **М 1:50**

План вентиляции

Стадия	Лист	Листов
П	64	129

выпуск 14.11.2026 № 32d0256903 · стр. 64 из 129

План отопления (М 1:75)

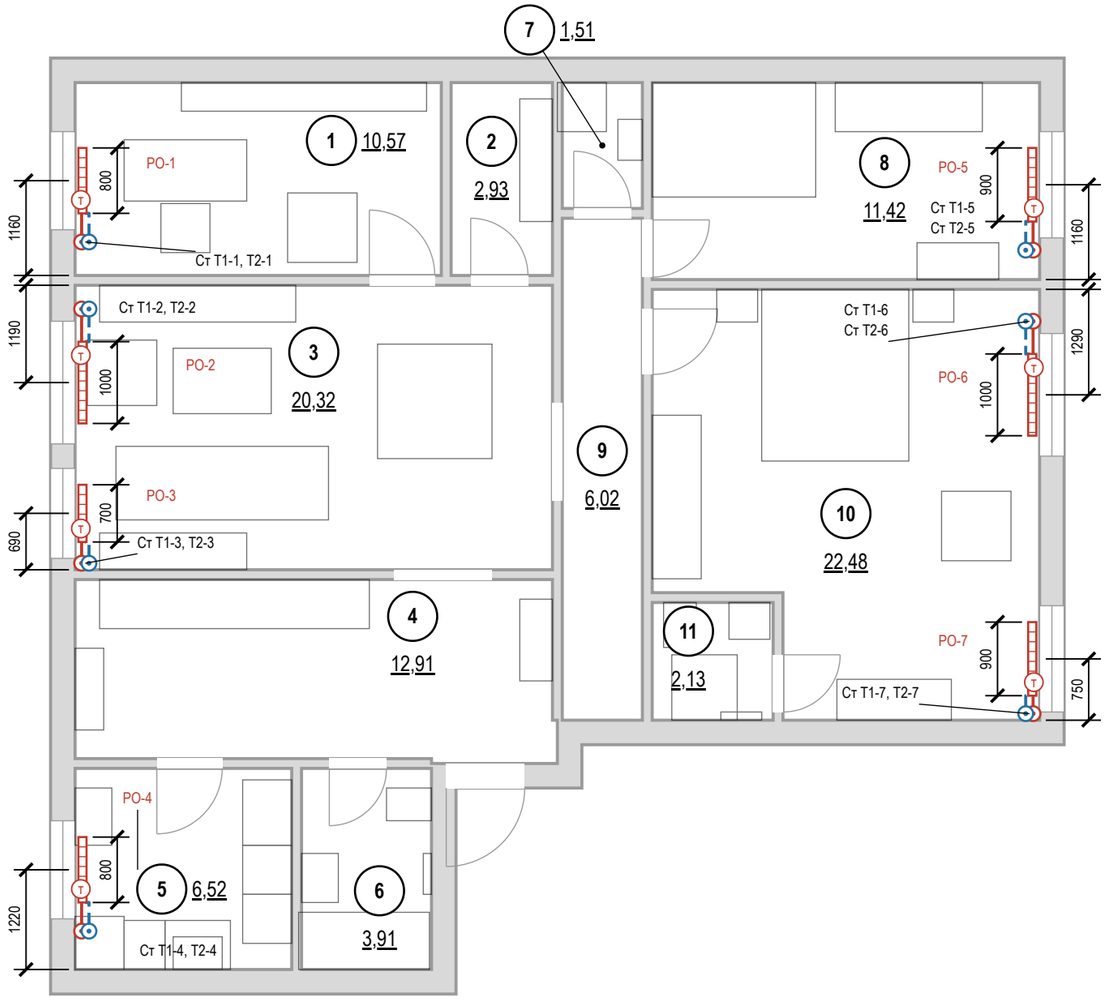

Условные обозначения

- 1 — номер помещения, площадь м²
- радиатор отопления (марка РО-N, длина по плану)
- клапан с термоголовкой на подаче
- стояк отопления, подающий (Ст Т1-N)
- стояк отопления, обратный (Ст Т2-N)
- Т1 — отопление, подающий трубопровод
- Т2 — отопление, обратный трубопровод

Ведомость радиаторов

Марка	Помещение	Тип	Д×В×Г, мм	Низ / стена	Q, Вт
РО-1	1. Кабинет-библиотека	панельный	800×400×100	120 / 40	расч.
РО-2	3. Гостиная-столовая	панельный	1000×400×100	120 / 40	расч.
РО-3	3. Гостиная-столовая	панельный	700×400×100	120 / 40	расч.
РО-4	5. Кухня	панельный	800×500×100	120 / 40	расч.
РО-5	8. Спальня 2	панельный	900×500×100	120 / 40	расч.
РО-6	10. Спальня мастер	панельный	1000×500×100	120 / 40	расч.
РО-7	10. Спальня мастер	панельный	900×500×100	120 / 40	расч.

тип и мощность — по теплотехническому расчёту
Низ — от чистого пола, стена — зазор до задней панели, мм.

Привязки — до обмера
Стояки отопления в исходных данных не заданы: показаны у откосов окон, подводки — принципиально. До черновых работ — обмер стояков и паспорта приборов; лист перевыпустить по факту.

Примечания

1. Расчёт системы отопления, теплопотерь и подбор приборов — проектная организация с допуском СРО; лист даёт места и привязки.
2. Тип, длина и мощность радиаторов — по теплотехническому расчёту; лист задаёт места, зазоры и подключение.
3. Радиаторы — под каждым окном жилых комнат и кухни, центр по оси проёма, длина 0,7 ширины окна (кратно 100); окончательно — по расчёту.
4. Зазоры радиатора: низ не менее 100 мм от чистого пола, верх не менее 100 мм до подоконника, 30–50 мм от стены до задней панели; центр по оси окна с допуском ±20 мм. Верх до подоконника — 215 мм (РО-1 — 200, РО-4 — 143, РО-5 — 163, РО-6 — 205, РО-7 — 205).
5. Радиаторы не закрывать глухими коробами и мебелью; перенос и замена приборов в многоквартирном доме — переустройство, согласование с управляющей организацией (ЖК РФ ст. 25–26); вынос на лоджию запрещён.
6. Трубы отопления через межквартирные стены не прокладывать (СП 51.13330.2011, п. 9.19); через перекрытия и перегородки — в гильзах.
7. Привязки приборов и подводок — по паспортам приобретённых радиаторов и клапанов, до черновых работ.
8. До закрытия отделкой трубопроводы отопления испытать гидростатическим давлением с оформлением акта (СП 73.13330.2016, 7.2–7.3).

	Лист	№ док.	Подпись	Дата	Проект: Квартира 103 м²	М 1:75
Дизайнер	Кырлан А.С.			14.11.26		
Проверил					План отопления	Стадия: П; Лист: 65; Листов: 129
Н. контр.						
Утв.						


выпуск 14.11.2026 № 32d0256903 · стр. 65 из 129

Спецификация плинтусов

Наименование	Помещения	Длина, м (с запасом)
Ultrawood Base 5340, ЛДФ под окраску, 83×15 мм, 2440 мм (арт. LDF-BASE-5340), крепление к стене, окраска в цвет Farrow & Ball No. 291	1, 3, 4, 5, 8, 9, 10	102
Ultrawood Base 5340, ЛДФ под окраску, 83×15 мм, 2440 мм (арт. LDF-BASE-5340), крепление к стене, окраска в цвет NCS S 0502-Y	2, 7	12

Отметки по высоте






±0,000	чистый пол пом. 1–5, 7–10; отсчёт высот
−0,015	чистый пол пом. 6, 11, ниже на 15 мм
−0,064	верх плиты — расчёт, не замер (задание на обмер)
сущ. пол	снимается до плиты; не замерен (задание на обмер)

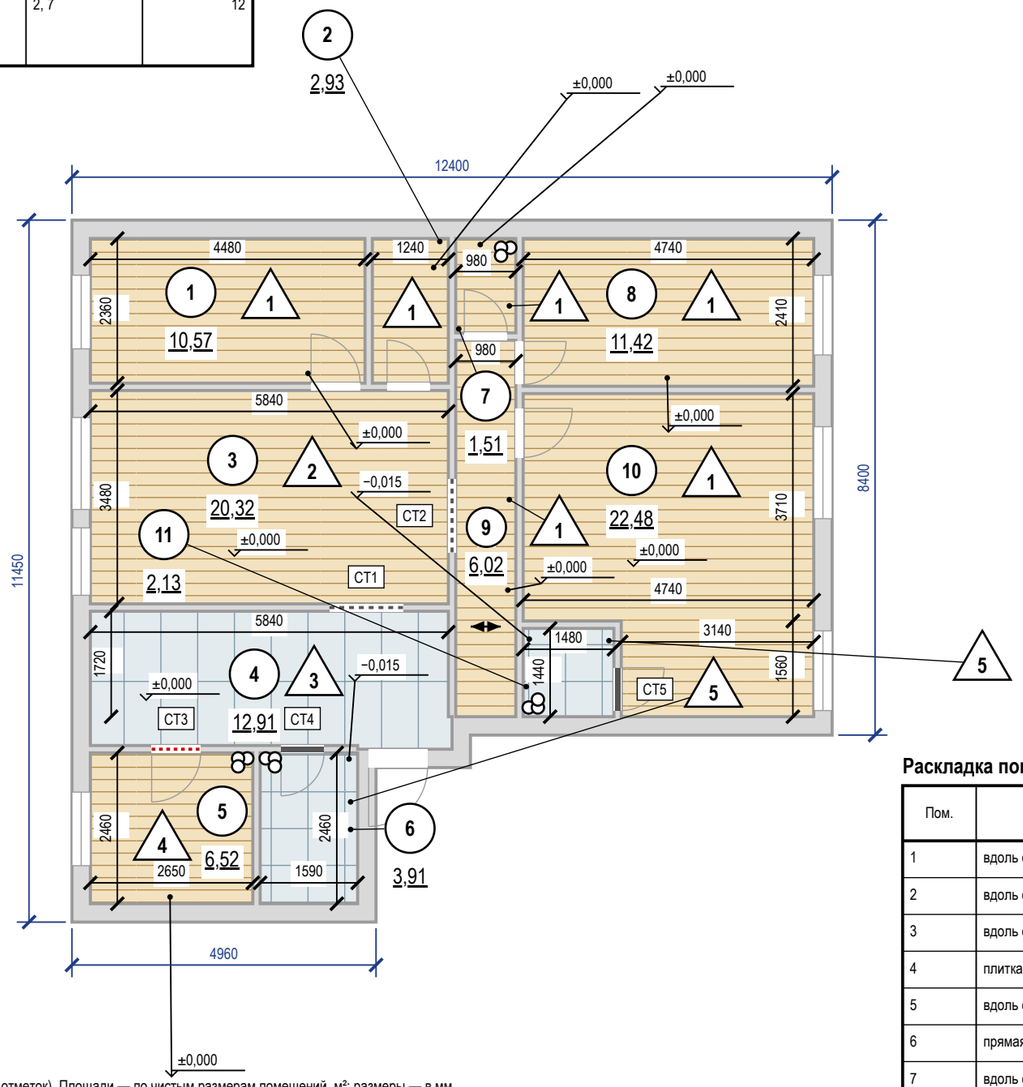

Примечания

1. За отметку ±0,000 принят чистый пол, не существующий (блок отметок). Площади — по чистым размерам помещений, м²; размеры — в мм.
2. Стык разнотипных покрытий — по оси дверного полотна (под полотном в закрытом положении); решение стыка — по ведомости стыков.
3. Размеры помещений в свету (ширина × длина, мм), не поместившиеся на плане: пом. 2 — 1240 × 2360; пом. 4 — 5840 × 1720, 5900 × 470, 1540 × 60; пом. 7 — 980 × 1540; пом. 9 — 980 × 6140.
4. Пол санузлов ниже смежных помещений на 15 мм за счёт меньшей толщины стяжки (верх плиты общий — по экспликации полов); гидроизоляция по стяжке с заведением на стены не менее 200 мм (СП 29.13330.2011, п. 7.2), до облицовки — тест проливом и акт скрытых работ.
5. Трубопроводы в конструкции пола не прокладываются: пирог пола 49–64 мм не вмещает выпуски канализации с уклоном — выпуски К1 ведутся по стенам над чистым полом в коробах (лист 39).
6. Звукоизоляционный слой под стяжкой проектом не предусмотрен (стяжка по плите): приведённый уровень ударного шума перекрытия с полом Lnw не более 60 дБ (СП 51.13330.2011, табл. 2) подтвердить по данным дома; при превышении — плавающая стяжка по звукоизоляции с демпферной лентой по контуру и у стояков, пирог пересчитать.
7. Штучные покрытия (инженерная доска): направление — по стрелке; влажность основания по СМ не более 2,0 % (по ТУ изготовителя).
8. Ровность основания — просвет под 2-метровой рейкой не более 2 мм: пом. 1, 2, 3, 5, 7, 8, 9, 10 (инженерная доска), пом. 4, 6, 11 (керамогранит); проверить до укладки покрытия (СП 71.13330.2017, табл. 8.5).
9. Сетка на плитке — условная, в размер формата; точка старта и раскладка — по листу раскладки плитки.
10. Узор покрытия (заливка-код типа пола) прерывается под надписями — площадями помещений и отметками чистого пола.
11. Пироги полов — по экспликации полов: слои сверху вниз, толщины в мм; гидроизоляция мокрых зон — в пироге и в ведомости отделки; схема пола — без масштаба.

Экспликация полов

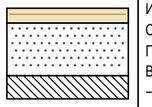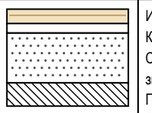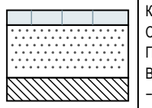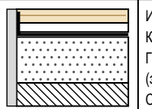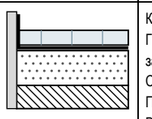
Номер помещения	Тип пола	Схема пола	Данные элементов пола (наименование, толщина, основание), мм	Площадь, м²
1, 2, 7, 8, 9, 10	1		Инженерная доска на клею — 14 Стяжка ЦПС М200 — 50 Плита перекрытия Всего 64 мм; ЧП ±0,000, верх плиты −0,064	54,93
3	2		Инженерная доска дуб на клею — 14 Клей паркетный МС-полимерный — 1 Стяжка ЦПС М300 (В22,5), фибра, по звукоизоляции — 49 Плита перекрытия монолитная Всего 64 мм; ЧП ±0,000, верх плиты −0,064	20,32
4	3		Керамогранит на клею C2 TE S1 — 14 Стяжка ЦПС М200 — 50 Плита перекрытия Всего 64 мм; ЧП ±0,000, верх плиты −0,064	12,91
5	4		Инженерная доска дуб на клею — 14 Клей паркетный МС-полимерный — 1 Гидроизоляция полиуретановая, 2 слоя (зона мойки и острова) — 2 Стяжка ЦПС М300 (В22,5), фибра, по звукоизоляции — 47 Плита перекрытия монолитная Всего 64 мм; ЧП ±0,000, верх плиты −0,064	6,52
6, 11	5		Керамогранит на клею C2 TE S1 — 14 Гидроизоляция обмазочная, 2 слоя, с заведением на стены 200 мм — 2 Стяжка ЦПС М200 — 33 Плита перекрытия Всего 49 мм; ЧП −0,015, верх плиты −0,064	6,04
			Итого	**100,72**

Раскладка покрытий


Пом.	Укладка	Старт (оси от чистовых стен), мм	Отступ 1-го ряда / крайние плитки, мм
1	вдоль стен A/B, прямая	от стены А, 1-й ряд вдоль неё	зазор от стены не задан
2	вдоль стен A/B, прямая	от стены А, 1-й ряд вдоль неё	зазор от стены не задан
3	вдоль стен A/B, прямая	от стены А, 1-й ряд вдоль неё	зазор от стены не задан
4	плитка	раскладка плиточника не задана	
5	вдоль стен A/B, прямая	от стены А, 1-й ряд вдоль неё	зазор от стены не задан
6	прямая, сетка 600×600, шов 2	ось X 771 от Г; ось Y 1206 от А	X 469 / 469; Y 302 / 302
7	вдоль стен A/B, прямая	от стены А, 1-й ряд вдоль неё	зазор от стены не задан
8	вдоль стен A/B, прямая	от стены А, 1-й ряд вдоль неё	зазор от стены не задан
9	вдоль стен A/B, прямая	от стены А, 1-й ряд вдоль неё	зазор от стены не задан
10	вдоль стен A/B, прямая	от стены А, 1-й ряд вдоль неё	зазор от стены не задан
11	прямая, сетка 600×600, шов 2	ось X 716 от Г; ось Y 696 от А	X 414 / 414; Y 394 / 394

	Лист	№ док.	Подпись	Дата	Проект: Квартира 103 м²	М 1:100		
Дизайнер	Кырлан А.С.			14.11.26	План покрытий пола	Стадия	Лист	Листов
Проверил						П	66	129
Н. контр.								
Утв.								

Фрагмент 1. Ванная (пом. 6). Пол 600×600, шов 2 мм (М 1:25)

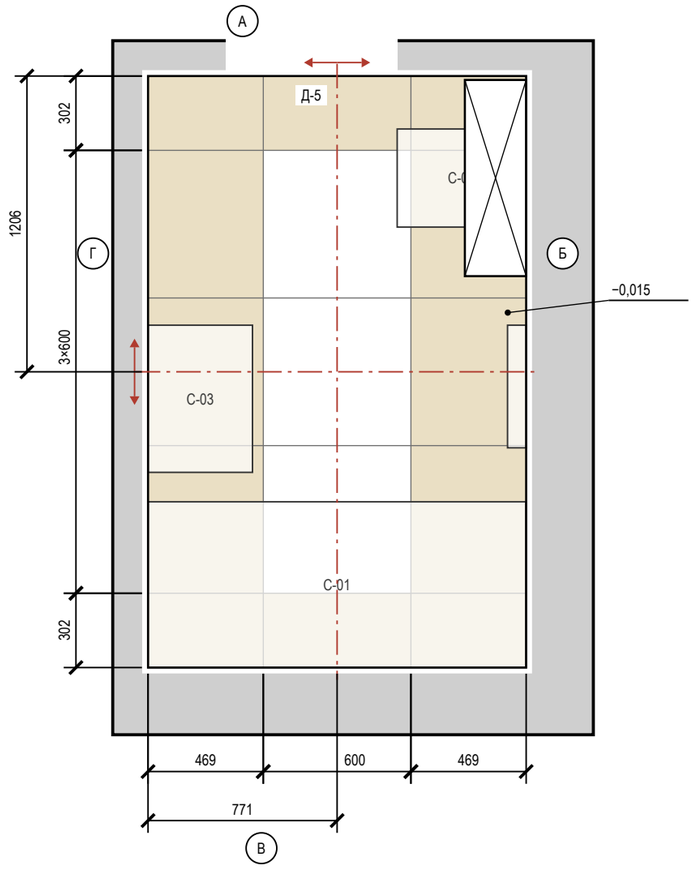

Фрагмент 2. Ванная мастер (пом. 11). Пол 600×600, шов 2 мм (М 1:25)

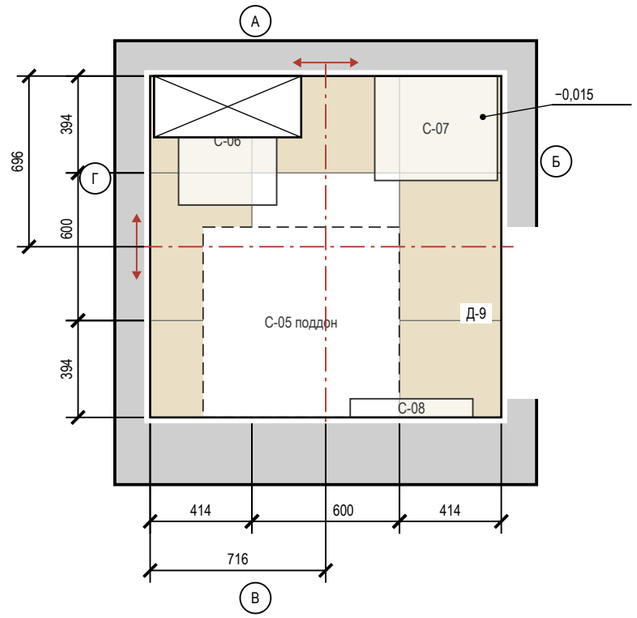

Ведомость материалов

Материал	Класс, код	Норма расхода	Кол-во
Затирка	CG2WA Mapei Ultracolor Plus 132	(a+b)/ab·шов·t·1,6	3,0 кг
Затирка	CG2WA	(a+b)/ab·шов·t·1,6	1,0 кг
Клей	C2 TE S1 Ceresit CM 17	1,2 кг/м²·мм, слой 5	238 кг (10 меш.)
Клей	C2 TE S1	1,2 кг/м²·мм, слой 5	84 кг (4 меш.)
Гидроизоляция	обмазочная, 2 слоя: пол, стены по периметру и зоны замачивания	по ТУ	18,7 м²
Демпф. лента	по периметру пола из плитки		27,1 м

Ведомость плитки

Помещение, поверхность	Плитка, код	Формат	Шов	S, м²	Целых	Подр.	С запасом
Ванная, пол	Atlas Concorde Marvel Travertine Sand Cross 60×60 Matte Sensitech, арт. AFUL (той же коллекции, что стены A8UZ; тон сверить по образцу)	600×600	2	3,91	3	12	17
Ванная, стены А–Г	A8UZ	600×1200	2	17,04	13	19	36
Ванная, короб инсталляции	A8UZ	600×1200	2	1,76	0	6	7
Ванная мастер, пол	Atlas Concorde Marvel Travertine Sand Cross 60×60 Matte Sensitech, арт. AFUL (той же коллекции, что стены A8UZ; тон сверить по образцу)	600×600	2	2,13	0	8	9
Ванная мастер, стены А–Г	A8UZ	600×1200	2	11,85	5	19	28
Ванная мастер, короб инсталляции	A8UZ	600×1200	2	1,47	1	3	5
Прихожая-холл, пол	A8UZ	600×1200	2	12,91	0	20	22
Итого 600×600				6,04	3	20	26
Итого 600×1200				**45,03**	**19**	**67**	**98**

Условные обозначения


- плитка целая; тонкая линия — шов
- плитка с подрезкой (размер — на цепочке)
- ось старта; стрелки — направление укладки
- сантехприбор: габарит, высота по практике
- поддон душа — плитку пола под ним не кладут
- короб инсталляции: плитка пола — до короба
- отметка чистого пола на полке выноски, м
- (А) обозначение стены А–Г (как на развёртках)

Примечания

1. Раскладка от чистовых размеров: стены санузлов теряют 10 + 5 + 9 = 24 мм на сторону (штукатурка, клей, плитка); подрезки — чистые, без шва.
2. Старт — от центра помещения (штрихпунктир, стрелки — направление укладки); размер старта — от чистовых стен Г и А.
3. Раскладка пола «Прихожая-холл» — на листе «Раскладка плитки. Прихожая-холл».
4. Калибр партии не задан — до укладки замерить (рабочий размер W, ГОСТ 13996-2019) и пересчитать подрезки.
5. Количество: целые по раскладке + по одной на подрезку, запас 10 %; один артикул — одна партия и тон. Исключены поддон, короб, проёмы и места за коробом; S — по чистым граням: стены нетто = зона облицовки по ведомости отделки − место за коробом инсталляции 1,68 м² (плитку за коробом не кладут), короб — отдельной строкой.
6. Клей C2 TE S1 Ceresit CM 17; C2 TE S1 (ГОСТ Р 56387-2018), затирка CG2WA Mapei Ultracolor Plus 132; CG2WA; расход — по ТУ выбранной марки.
7. Гидроизоляция: пол и стены 200 мм от ЧП; над ванной — до 2000 и 300 мм за борт (пом. 6), у душа — до 2000 и 500 мм за поддон (пом. 11) (см. развёртки); акт скрытых работ, пролив 24 ч.
8. Швы пола совмещены со швами стены А; по периметру — демпферная лента.
9. Отметка чистого пола −0,015, порог 15 мм; стык с соседним покрытием — по оси полотна двери.

	Лист	№ док.	Подпись	Дата	Проект: Квартира 103 м²			М 1:25
Дизайнер	Кырлан А.С.			14.11.26	Раскладка плитки. Планы полов	Стадия	Лист	Листов
Проверил						П	67	129
Н. контр.								
Утв.								

Фрагмент 1. Прихожая-холл (пом. 4). Пол 600×1200, шов 2 мм (М 1:20)

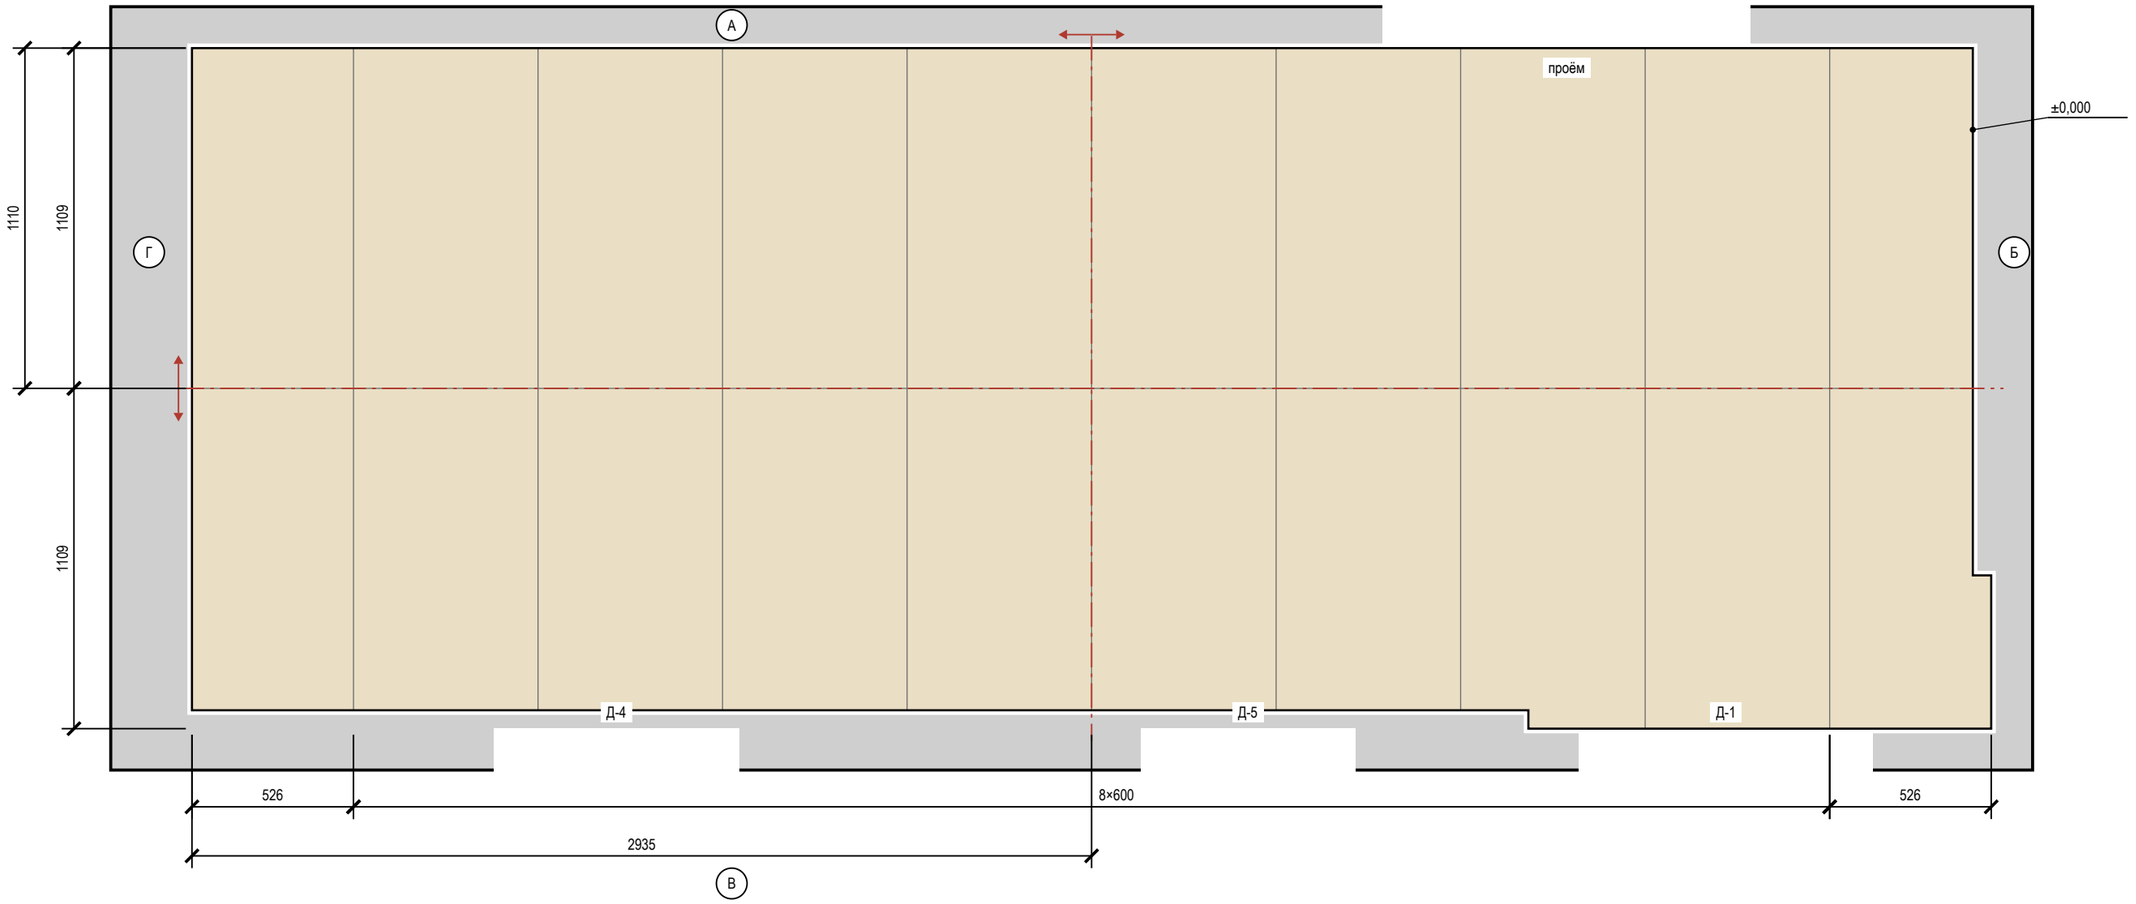

Условные обозначения

- плитка целая; тонкая линия — шов
- плитка с подрезкой (размер — на цепочке)
- ось старта; стрелки — направление укладки
- отметка чистого пола на полке выноски, м
- (А) обозначение стены А–Г (как на развёртках)

Подсчёт плитки

Поверхность	Формат	S, м²	Целых	Подр.	С запасом
Прихожая-холл, пол	600×1200	12,91	0	20	22

Примечания

1. Прихожая-холл: керамогранит 600×1200, длинная сторона — вдоль стен Б и Г, шов 2 мм, прямая раскладка от центра. Стены окрашены: раскладка от чистового контура минус штукатурка и шпаклёвка 15 мм на сторону (принято); подрезки 526 / 1109 мм, срез — под плинтус.
2. Прихожая-холл: деформационный зазор по периметру 8–10 мм под плинтусом; в проёмах — стык с соседним покрытием по оси полотна двери. Клей C2 TE S1, затирка CG2WA.
3. Клей, затирка и итог по форматам — в ведомостях листа «Раскладка плитки. Планы полов».

	Лист	№ док.	Подпись	Дата	Проект: Квартира 103 м²			М 1:20
Дизайнер	Кырлан А.С.			14.11.26	Раскладка плитки. Прихожая-холл	Стадия	Лист	Листов
Проверил						П	68	129
Н. контр.								
Утв.								

выпуск 14.11.2026 № 32d0256903 · стр. 68 из 129

Стена А (М 1:20)


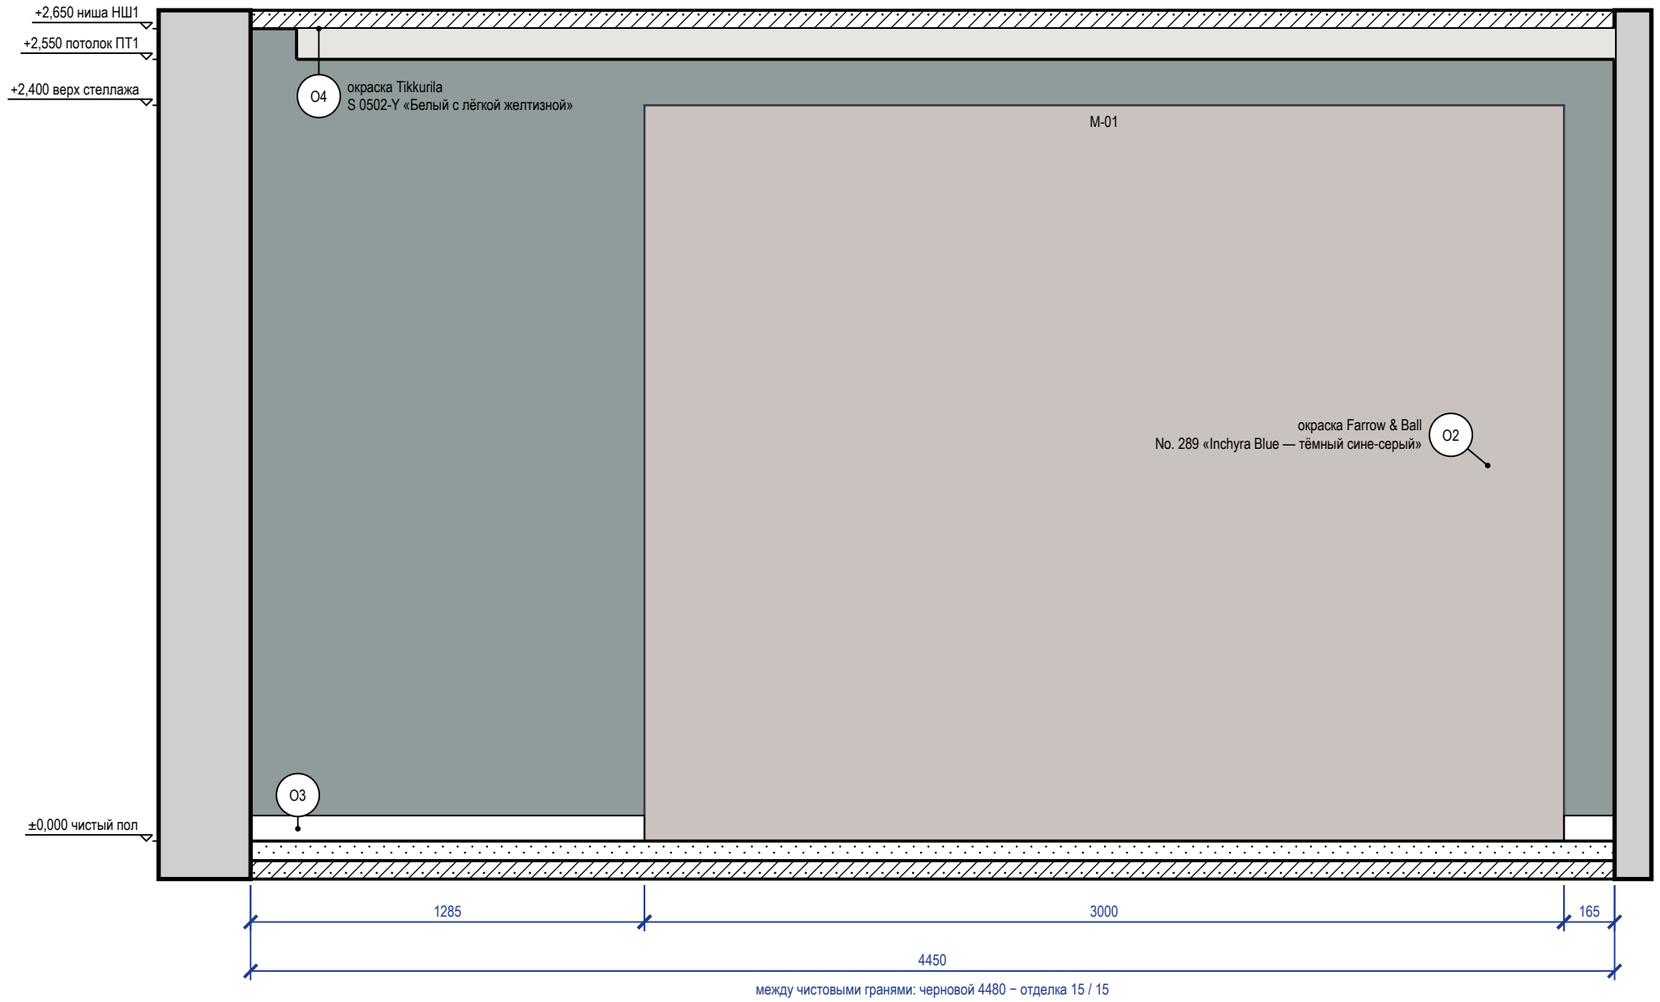


Схема развёрток (М 1:50)



Стена А — визуализация, лист 3

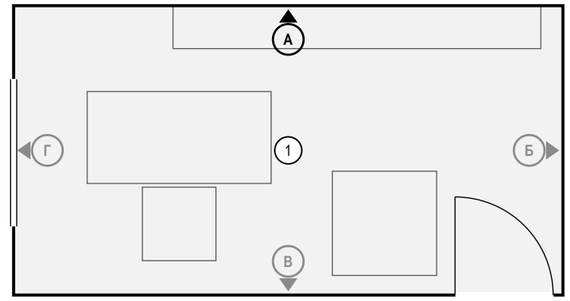

Ведомость отделки (на листе)

Марка	Поверхность	Материал, изделие	Цвет, код	Кол.
О2	акцентная стена	окраска, Farrow & Ball Modern Emulsion, матовая, подготовка Q3	Farrow & Ball No. 289 «Inchyra Blue — тёмный сине-серый»	11,8 м²
О3	плинтус	плинтус МДФ, h 83 мм, Ultrawood Base 5340, ЛДФ под окраску, 83×15 мм, 2440 мм (арт. LDF-BASE-5340)	Farrow & Ball No. 291 «School House White — тёплый меловой белый»	1,4 м
О4	потолок	окраска, Tikkurila Anti-Reflex 2, глубокоматовая, подготовка Q3	NCS S 0502-Y «Белый с лёгкой желтизной»	10,6 м²

Ведомость изделий и проёмов (на листе)

Марка	Изделие, проём	На виде Ш×В, мм	Низ, мм
М-01	стеллаж-библиотека из ореха на всю стену, латунные полкодержатели	3000×2400	0

Примечания

1. Размеры — в мм от чистовых поверхностей стен; условные обозначения и общие указания — лист 22.

	Лист	№ док.	Подпись	Дата
Дизайнер	Кырлан А.С.			14.11.26
Проверил				
Н. контр.				
Утв.				


Проект: Квартира 103 м² — **М 1:20**

Развёртка стены А. Кабинет-библиотека (пом. 1)

Стадия	Лист	Листов
П	69	129

выпуск 14.11.2026 № 32d0256903 · стр. 69 из 129

Стена Б (М 1:20)

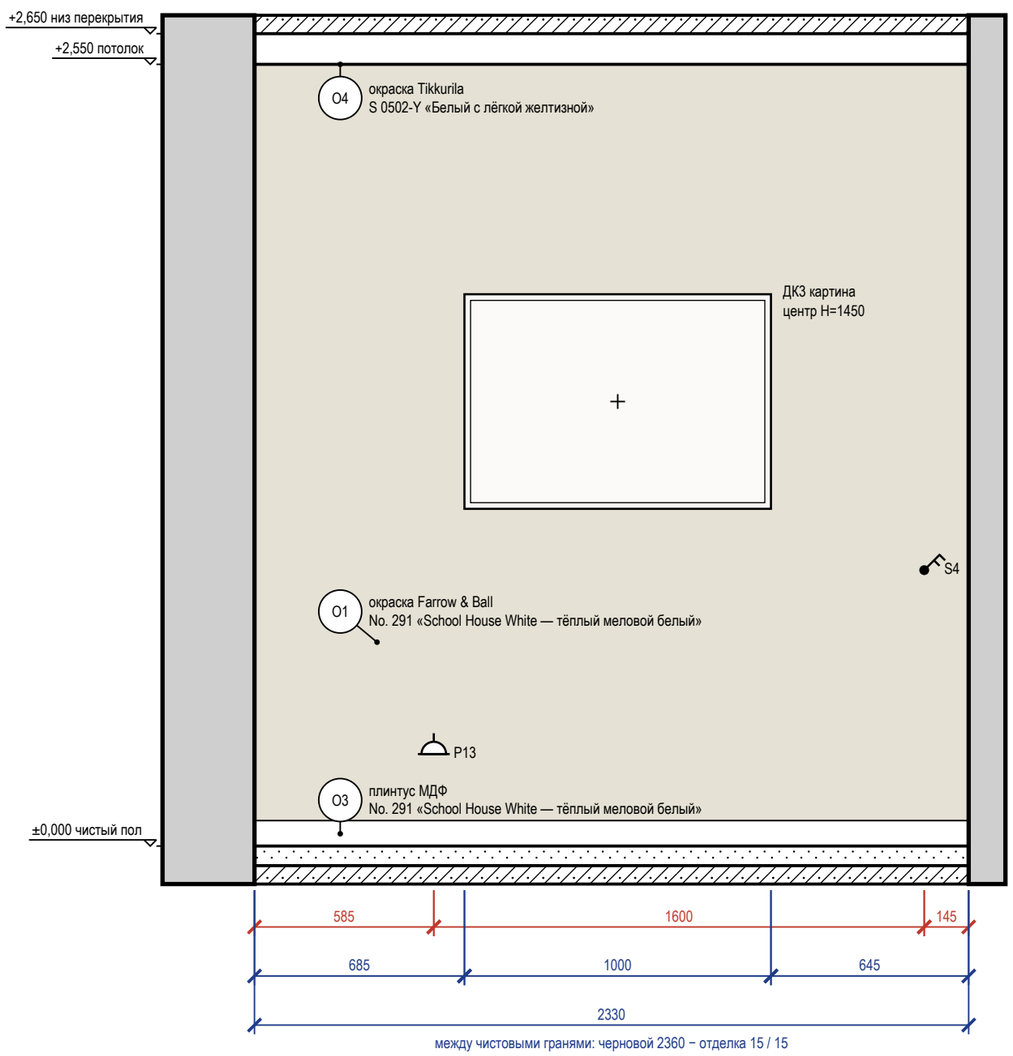

Ведомость точек и выводов

Марка	Что это	Гр.	H, мм	От угла, мм	Примечание
Р13	розетка: уборка	5	300	585	
S4	выключатель	1	900	2185	

Ведомость изделий и проёмов (на листе)

Марка	Изделие, проём	На виде Ш×В, мм	Низ, мм
ДК3	картина	1000×700	1100

Примечания

1. Размеры — в мм от чистовых поверхностей стен; условные обозначения и общие указания — лист 22.
2. Картины и зеркала крепить к основанию по паспорту изделия (закладные и анкеры — в перечне скрытых работ); крест — ось центра предмета.


Стена Б — визуализация, лист 4



Ведомость отделки (на листе)

Марка	Поверхность	Материал, изделие	Цвет, код	Кол.
О1	стены	окраска, Farrow & Ball Modern Emulsion, матовая, подготовка Q3	Farrow & Ball No. 291 «School House White — тёплый меловой белый»	5,9 м²
О3	плинтус	плинтус МДФ, h 83 мм, Ultrawood Base 5340, ЛДФ под окраску, 83×15 мм, 2440 мм (арт. LDF-BASE-5340)	Farrow & Ball No. 291 «School House White — тёплый меловой белый»	2,3 м
О4	потолок	окраска, Tikkurila Anti-Reflex 2, глубокоматовая, подготовка Q3	NCS S 0502-Y «Белый с лёгкой желтизной»	10,6 м²

Схема развёрток (М 1:50)

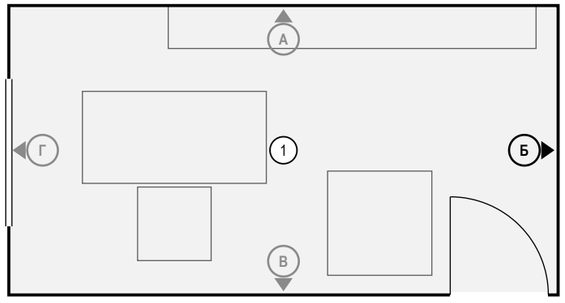

	Лист	№ док.	Подпись	Дата
Дизайнер	Кырлан А.С.			14.11.26
Проверил				
Н. контр.				
Утв.				

Проект: Квартира 103 м² — **М 1:20**

Развёртка стены Б.
Кабинет-библиотека (пом. 1)

Стадия	Лист	Листов
П	70	129

выпуск 14.11.2026 № 32d0256903 · стр. 70 из 129

Стена В (М 1:20)


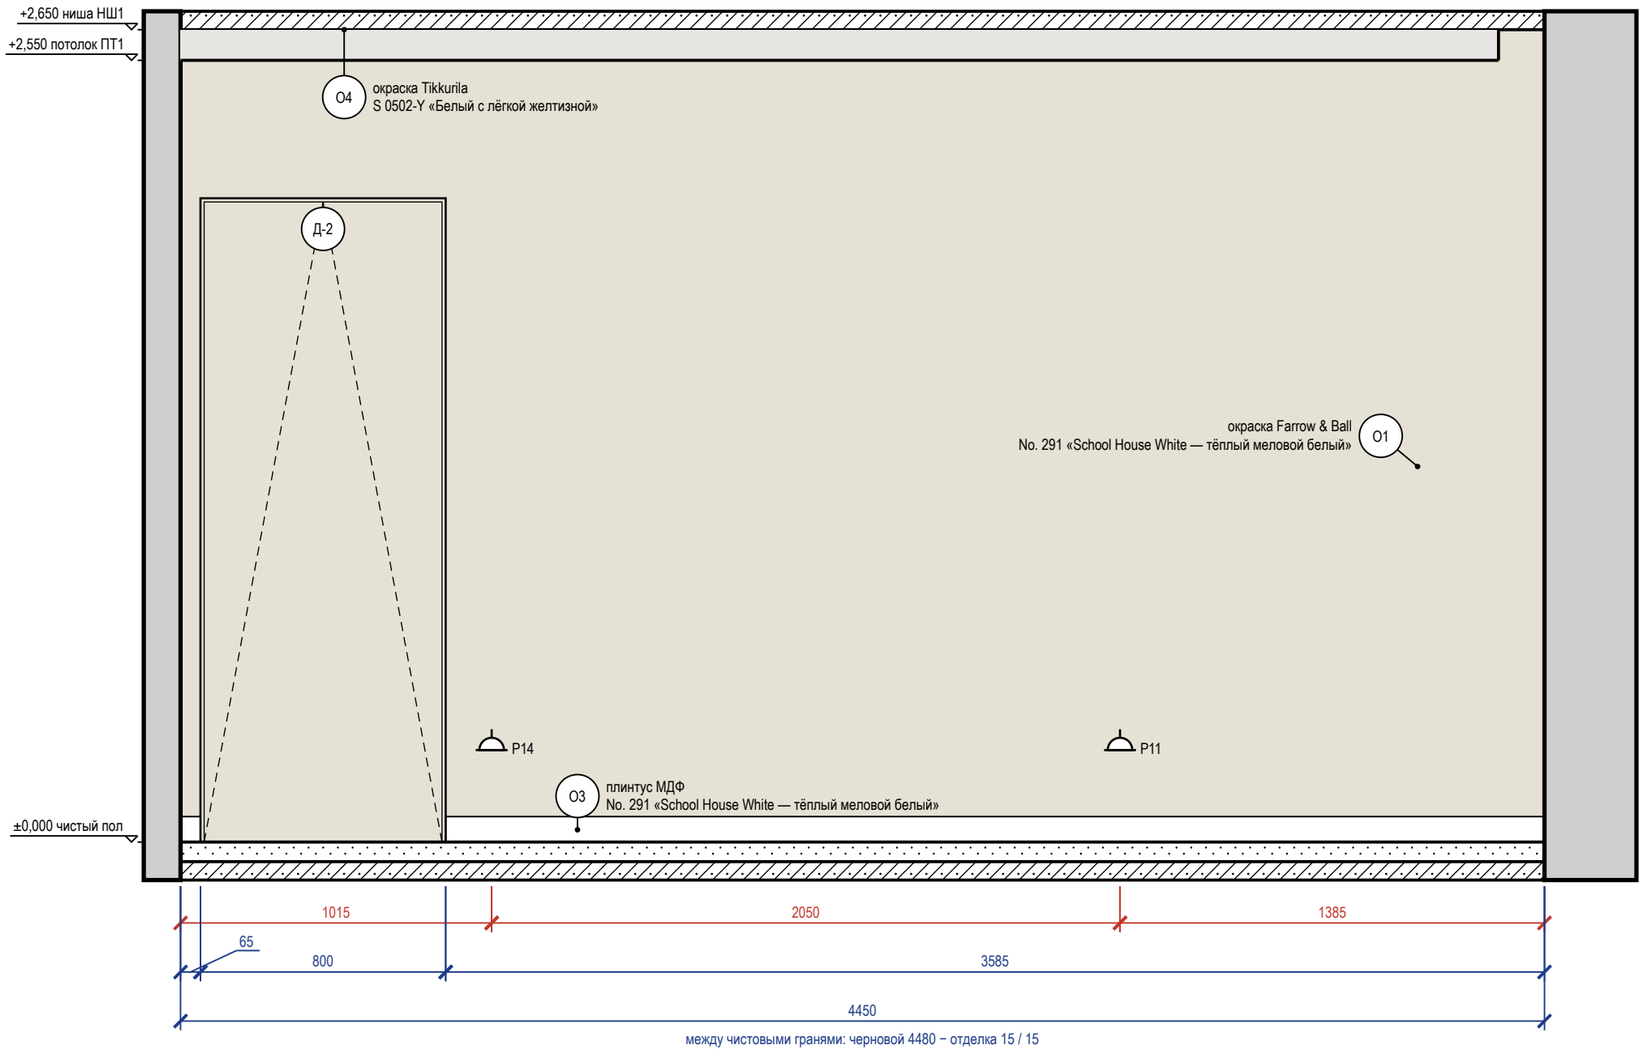


Схема развёрток (М 1:50)

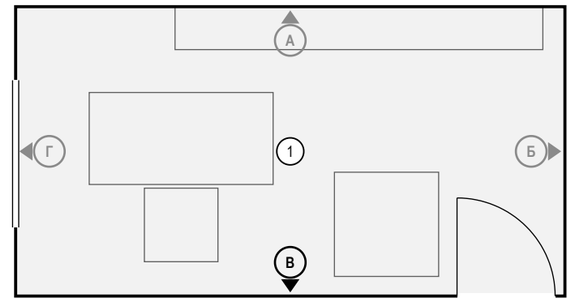

Ведомость точек и выводов

Марка	Что это	Гр.	Н, мм	От угла, мм	Примечание
Р14	розетка: уборка у входа	5	300	1015	
Р11	розетка: общего назначения	5	300	3065	

Ведомость изделий и проёмов (на листе)

Марка	Изделие, проём	На виде Ш×В, мм	Низ, мм
Д-2	дверь скрытого монтажа	800×2100	0

Ведомость отделки (на листе)

Марка	Поверхность	Материал, изделие	Цвет, код	Кол.
О1	стены	окраска, Farrow & Ball Modern Emulsion, матовая, подготовка Q3	Farrow & Ball No. 291 «School House White тёплый меловой белый»	10,1 м²
О3	плинтус	плинтус МДФ, h 83 мм, Ultrawood Base 5340, ЛДФ под окраску, 83×15 мм, 2440 мм (арт. LDF-BASE-5340)	Farrow & Ball No. 291 «School House White тёплый меловой белый»	3,6 м
О4	потолок	окраска, Tikkurila Anti-Reflex 2, глубокоматовая, подготовка Q3	NCS S 0502-Y «Белый с лёгкой желтизной»	10,6 м²

Примечания

1. Размеры — в мм от чистовых поверхностей стен; условные обозначения и общие указания — лист 22.
2. Двери скрытого монтажа — полотно в плоскости стены, отделка стены по полотну, плинтус прерывается у короба (узел — на листе узлов).

	Лист	№ док.	Подпись	Дата
Дизайнер	Кырлан А.С.			14.11.26
Проверил				
Н. контр.				
Утв.				


Проект: Квартира 103 м² — **М 1:20**

Развёртка стены В.
Кабинет-библиотека (пом. 1)


Стадия	Лист	Листов
П	71	129

выпуск 14.11.2026 № 32d0256903 · стр. 71 из 129

Стена Г (М 1:20)

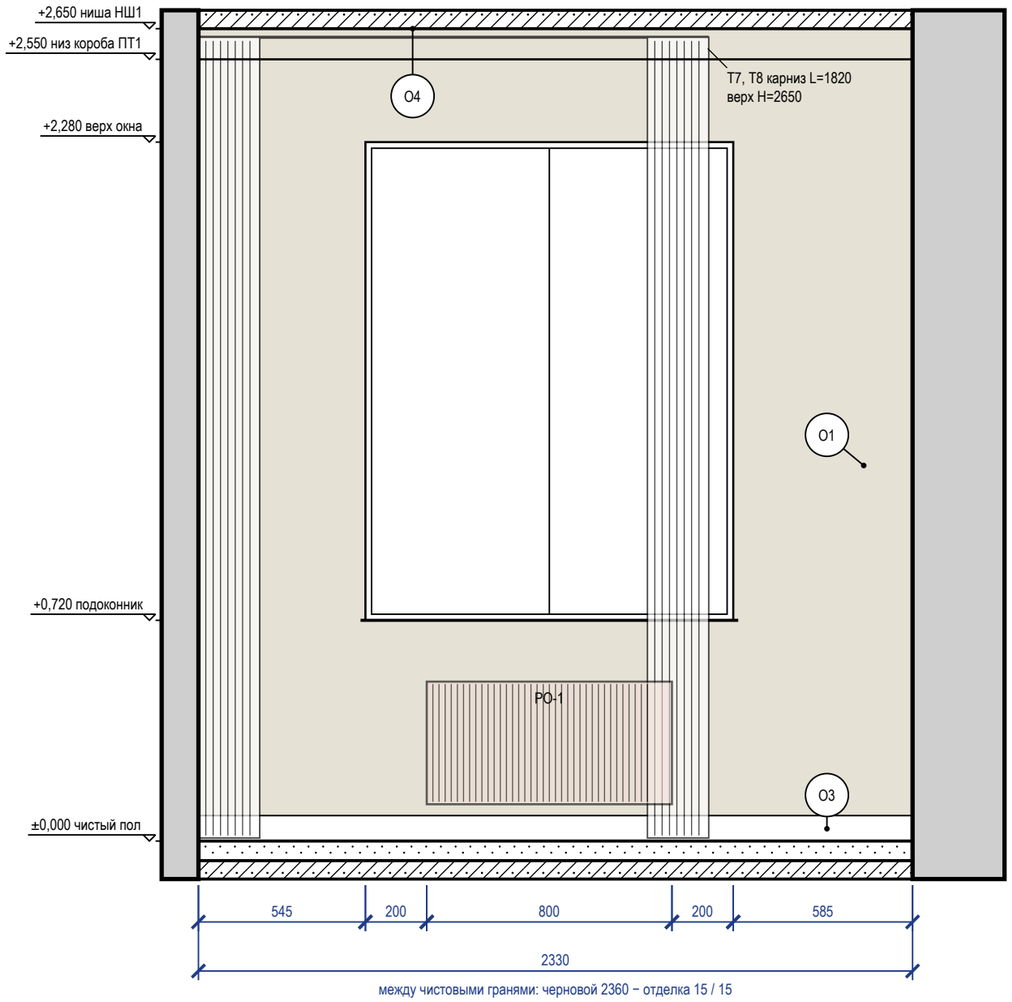


Стена Г — визуализация, лист 5

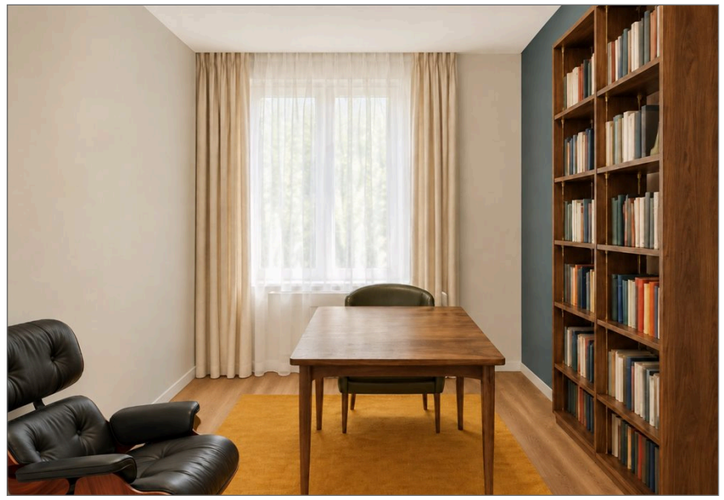

Ведомость отделки (на листе)

Марка	Поверхность	Материал, изделие	Цвет, код	Кол.
О1	стены	окраска, Farrow & Ball Modern Emulsion, матовая, подготовка Q3	Farrow & Ball No. 291 «School House White — тёплый меловой белый»	4,3 м²
О3	плинтус	плинтус МДФ, h 83 мм, Ultrawood Base 5340, ЛДФ под окраску, 83×15 мм, 2440 мм (арт. LDF-BASE-5340)	Farrow & Ball No. 291 «School House White — тёплый меловой белый»	2,3 м
О4	потолок	окраска, Tikkurila Anti-Reflex 2, глубокоматовая, подготовка Q3	NCS S 0502-Y «Белый с лёгкой желтизной»	10,6 м²

Схема развёрток (М 1:50)

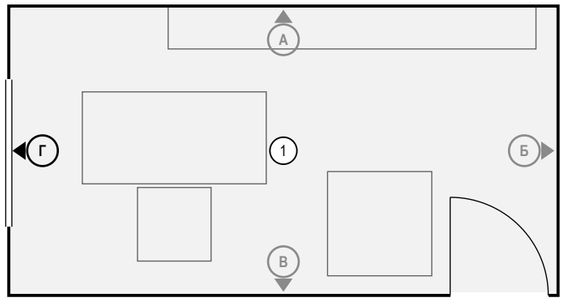


Ведомость изделий и проёмов (на листе)

Марка	Изделие, проём	На виде Ш×В, мм	Низ, мм
РО-1	радиатор отопления	800×400	120

5 **Плинтус МДФ 83×15 мм у окрашенной стены по доске (ламинату) (М 1:10)**

Узел 5 — лист С13

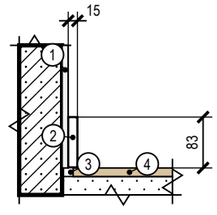

Поз.	Состав слоя, изделие
1	штукатурка, шпаклёвка Q3, окраска — по ведомости отделки
2	плинтус МДФ 83×15 под окраску в цвет стены; клей монтажный — к стене, не к полу
3	зазор покрытия у стены 8–10 мм закрывается плинтусом
4	инженерная доска дуб на клею


Примечания

1. Размеры — в мм от чистовых поверхностей стен; условные обозначения и общие указания — лист 22.
2. Карнизы (шины) — по ведомости текстиля декоратора: длина L и верх H на развёртке — те же числа, что в ведомости; крепление — до окраски потолка.
3. Карниз Т7, Т8: по ведомости текстиля шина L=1820 мм, а от её начала до чистового угла стены — 1665 мм: шина не встаёт, длину согласовать с декоратором до заказа.
4. Линии узора (швы плитки, складки штор, рёбра радиаторов) прерываются у знаков и выносок — просвет между линиями не менее 0,7 мм.


	Лист	№ док.	Подпись	Дата	Проект: Квартира 103 м²			М 1:20
Дизайнер	Кырлан А.С.			14.11.26	Развёртка стены Г. Кабинет-библиотека (пом. 1)	Стадия	Лист	Листов
Проверил						П	72	129
Н. контр.								
Утв.								

выпуск 14.11.2026 № 32d0256903 · стр. 72 из 129

Стена Б (М 1:20)

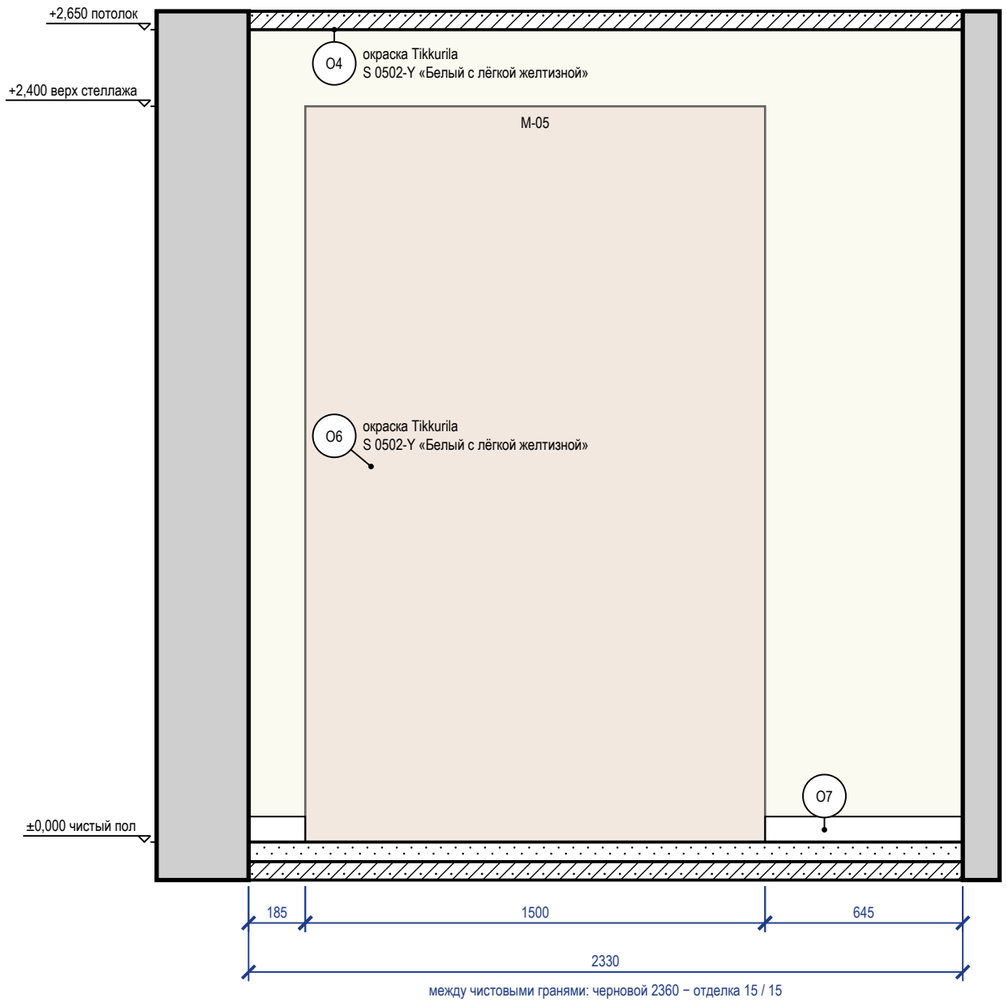

Стена В (М 1:20)

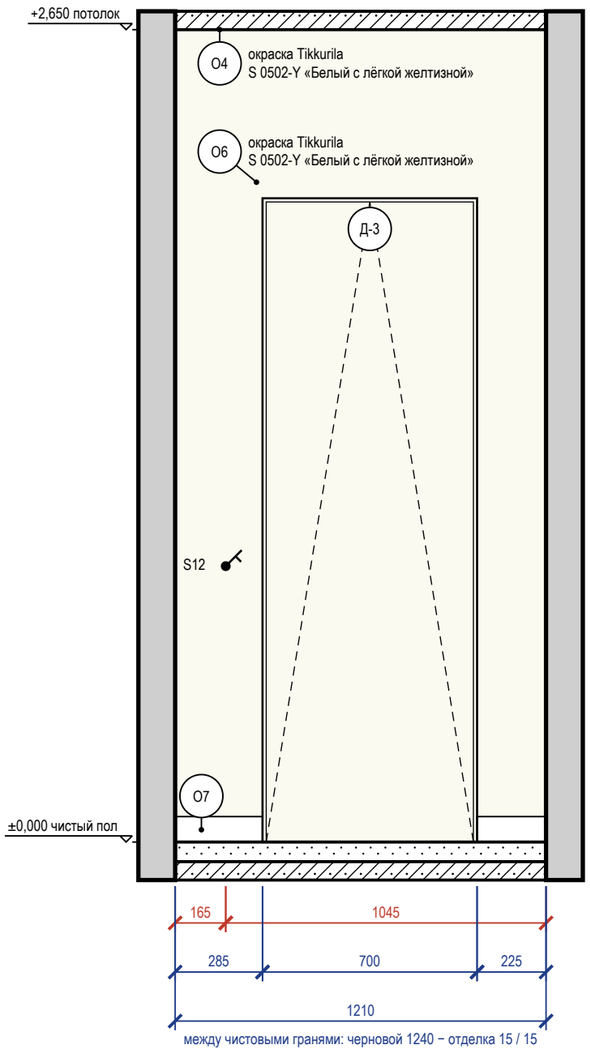

Стена Б — визуализация, лист 6


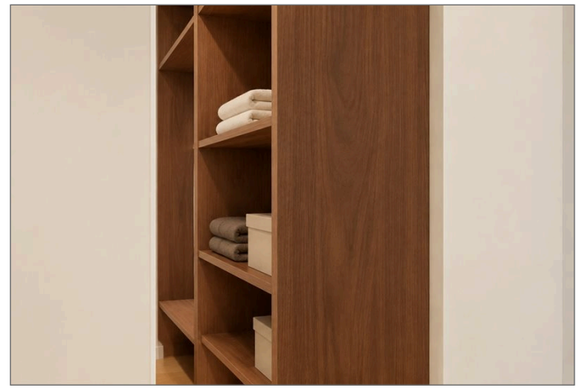


Схема развёрток (М 1:50)

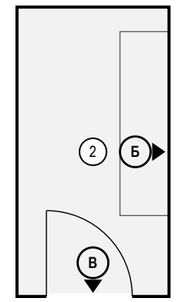

Ведомость точек и выводов

Стена	Марка	Что это	Гр.	Н, мм	От угла, мм	Примечание
В	S12	выключатель	1	900	165	

Ведомость изделий и проёмов (на листе)

Стена	Марка	Изделие, проём	На виде Ш×В, мм	Низ, мм
Б	М-05	стеллаж для хранения	1500×2400	0
В	Д-3	дверь скрытого монтажа	700×2100	0

Ведомость отделки (на листе)

Марка	Поверхность	Материал, изделие	Цвет, код	Кол.
О4	потолок	окраска, Tikkurila Anti-Reflex 2, глубокоматовая, подготовка Q3	NCS S 0502-Y «Белый с лёгкой желтизной»	2,9 м²
О6	стены	окраска, Tikkurila Harmony, матовая, подготовка Q3	NCS S 0502-Y «Белый с лёгкой желтизной»	7,9 м²
О7	плинтус	плинтус МДФ, h 83 мм, Ultrawood Base 5340, ЛДФ под окраску, 83×15 мм, 2440 мм (арт. LDF-BASE-5340)	NCS S 0502-Y «Белый с лёгкой желтизной»	1,3 м

Примечания

1. Размеры — в мм от чистовых поверхностей стен; условные обозначения и общие указания — лист 22.
2. Двери скрытого монтажа — полотно в плоскости стены, отделка стены по полотну, плинтус прерывается у короба (узел — на листе узлов).

	Лист	№ док.	Подпись	Дата
Дизайнер	Кырлан А.С.			14.11.26
Проверил				
Н. контр.				
Утв.				


Проект: Квартира 103 м² — **М 1:20**

Развёртки стен. Кладовая (пом. 2)

Стадия	Лист	Листов
П	73	129

выпуск 14.11.2026 № 32d0256903 · стр. 73 из 129

Стена А (М 1:20)

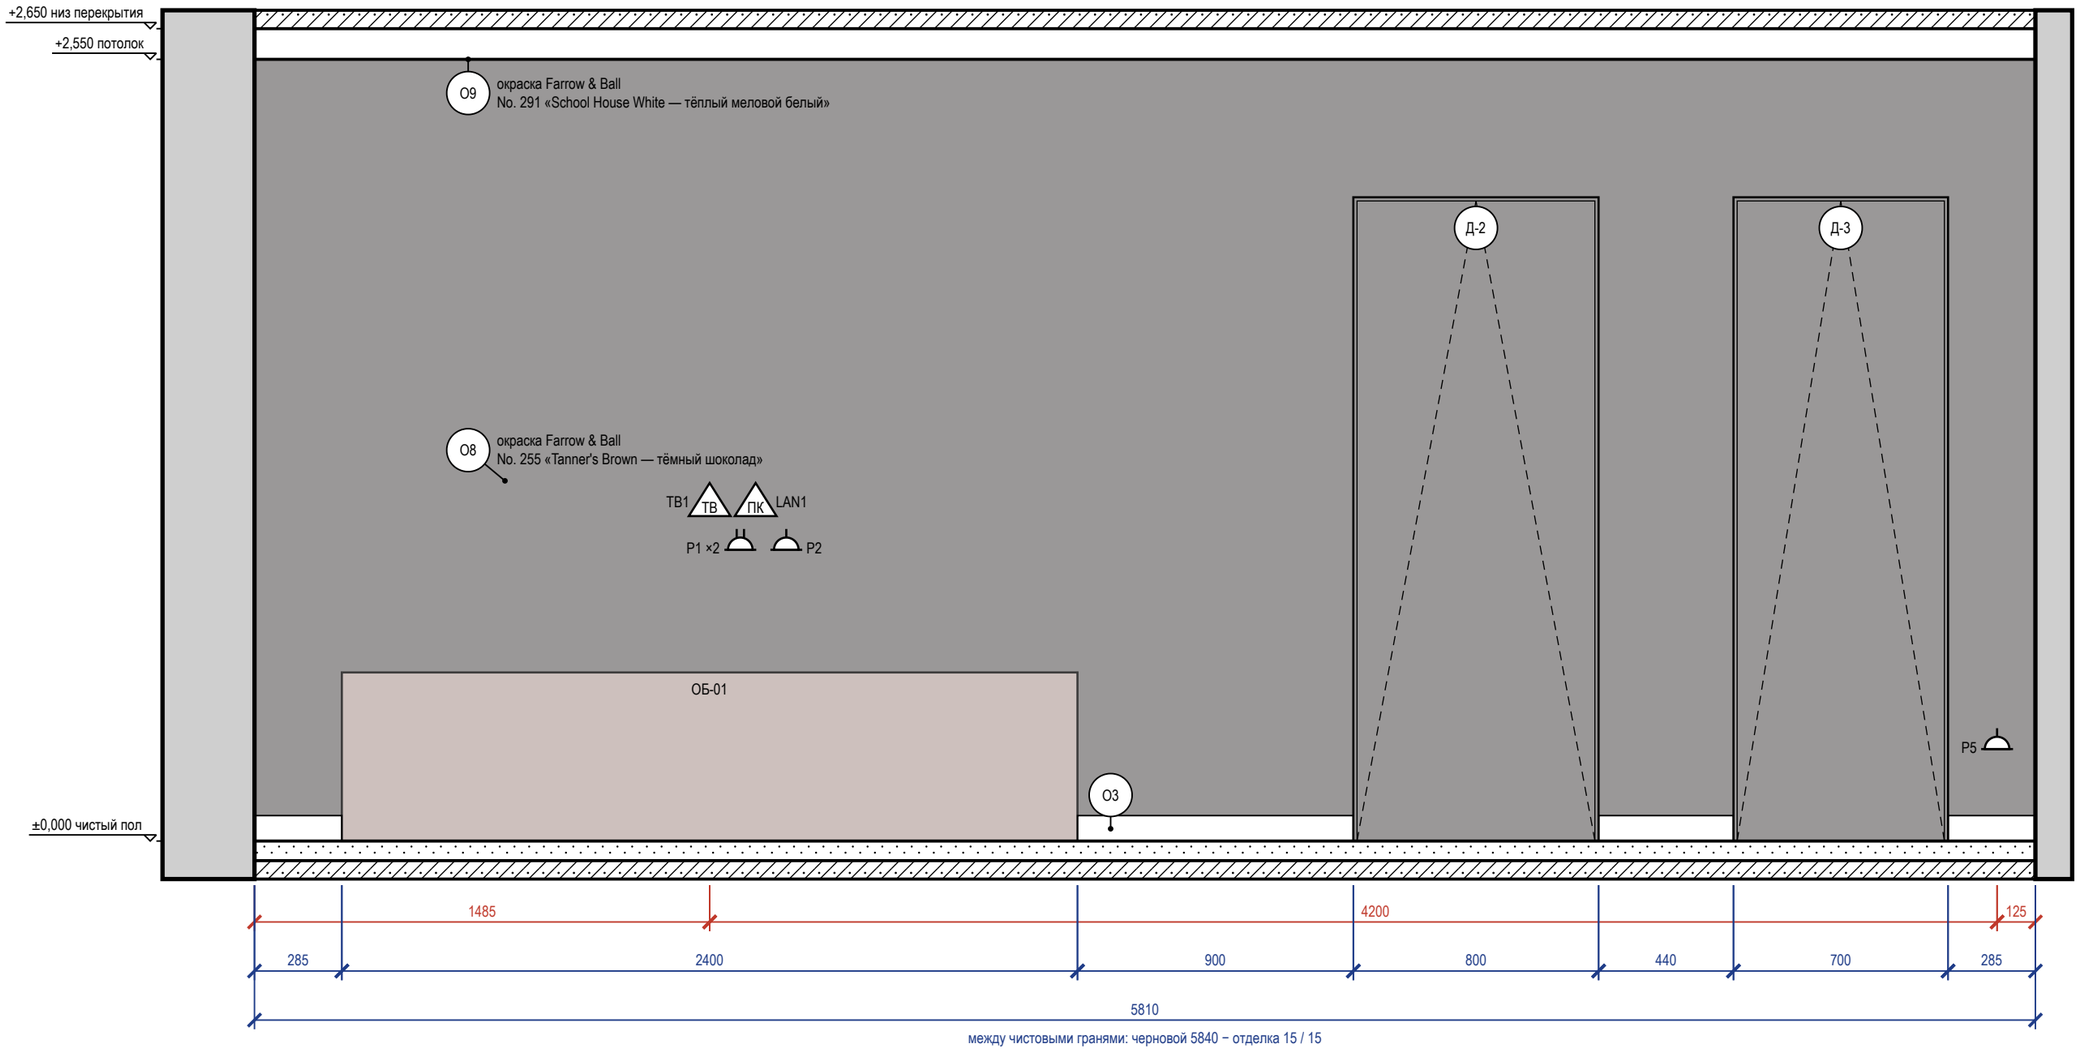


Ведомость точек и выводов

Марка	Что это	Гр.	Н, мм	От угла, мм	Примечание
ТВ1	розетка ТВ: ТВ-зона		1100	1485	
Р1	розетка: ТВ-зона: телевизор, медиаплеер	5	950	1585	рамка 2 поста
LAN1	розетка RJ45: ТВ-зона: Smart TV		1100	1635	
Р2	розетка: ТВ-зона: саундбар	5	950	1735	
Р5	розетка: обеденная зона, буфет М-10	5	300	5685	

Ведомость отделки (на листе)

Марка	Поверхность	Материал, изделие	Цвет, код	Кол.
О3	плинтус	плинтус МДФ, h 83 мм, Ultrawood Base 5340, ЛДФ под окраску, 83×15 мм, 2440 мм (арт. LDF-BASE-5340), полуглянцевая	Farrow & Ball No. 291 «School House White тёплый меловой белый»	1,9 м
О8	акцентная стена	окраска, Farrow & Ball Modern Emulsion, аналог: интерьерная краска Farrow & Ball Modern Emulsion в цвете веера No. 255, матовая, матовая, подготовка К3	Farrow & Ball No. 255 «Tanner's Brown — тёмный шоколад»	11,7 м²
О9	потолок	окраска, Farrow & Ball Modern Emulsion, матовая, подготовка Q3	Farrow & Ball No. 291 «School House White тёплый меловой белый»	20,3 м²

Схема развёрток (М 1:100)

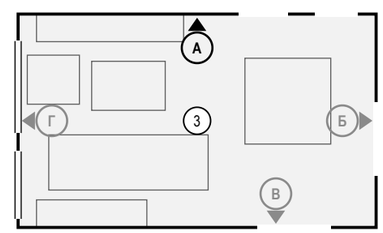

Примечания

1. Размеры — в мм от чистовых поверхностей стен; условные обозначения и общие указания — лист 22.
2. Двери скрытого монтажа — полотно в плоскости стены, отделка стены по полотну, плинтус прерывается у короба (узел — на листе узлов).

	Лист	№ док.	Подпись	Дата
Дизайнер	Кырлан А.С.			14.11.26
Проверил				
Н. контр.				
Утв.				


Проект: Квартира 103 м² — **М 1:20**

Развёртка стены А.
Гостиная-столовая (пом. 3)

Стадия	Лист	Листов
П	74	129

выпуск 14.11.2026 № 32d0256903 · стр. 74 из 129

Стена Б (М 1:20)

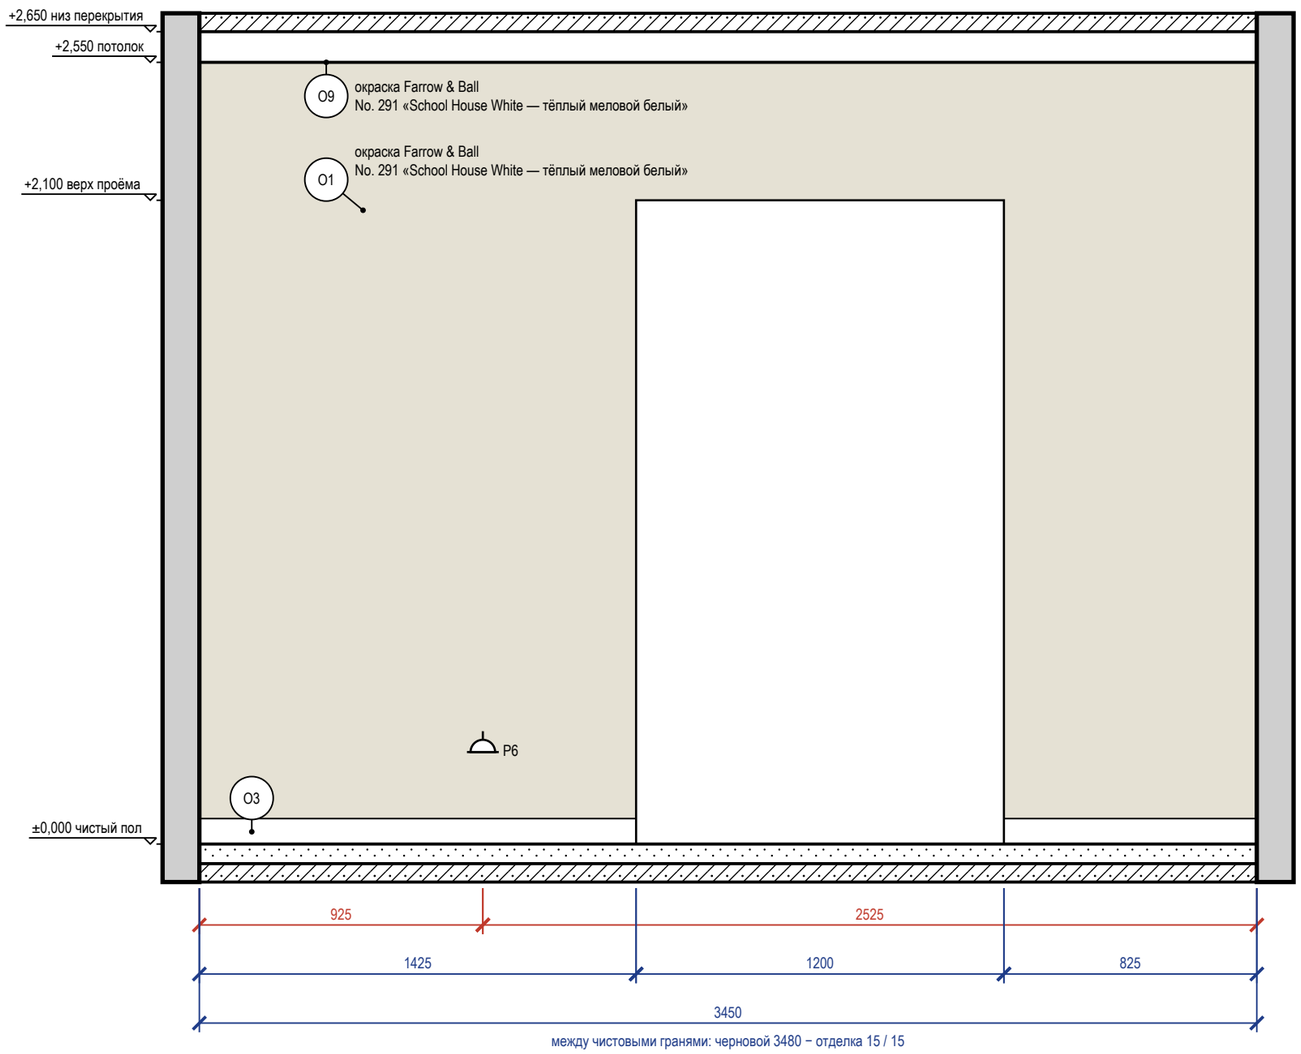


Ведомость точек и выводов

Марка	Что это	Гр.	Н, мм	От угла, мм	Примечание
Р6	розетка: уборка	5	300	925	


Ведомость отделки (на листе)

Марка	Поверхность	Материал, изделие	Цвет, код	Кол.
О1	стены	окраска, Farrow & Ball Modern Emulsion, матовая, подготовка К3	Farrow & Ball No. 291 «School House White — тёплый меловой белый»	6,3 м²
О3	плинтус	плинтус МДФ, h 83 мм, Ultrawood Base 5340, ЛДФ под окраску, 83×15 мм, 2440 мм (арт. LDF-BASE-5340), полуглянцевая	Farrow & Ball No. 291 «School House White — тёплый меловой белый»	2,3 м
О9	потолок	окраска, Farrow & Ball Modern Emulsion, матовая, подготовка Q3	Farrow & Ball No. 291 «School House White — тёплый меловой белый»	20,3 м²

Схема развёрток (М 1:50)

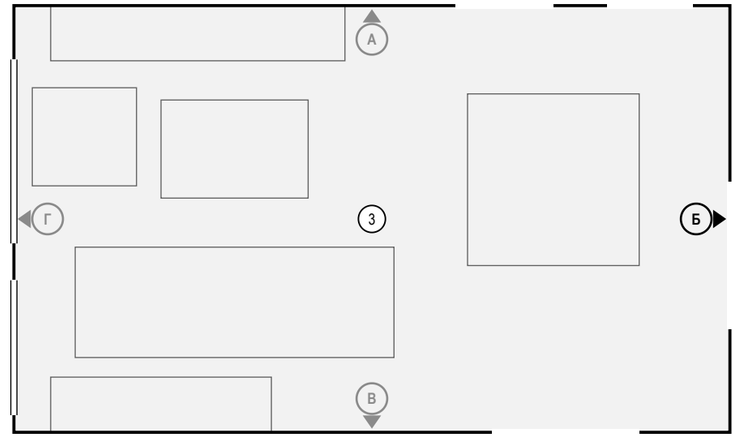

5 **Плинтус МДФ 83×15 мм у окрашенной стены по доске (ламинату) (М 1:10)**
Узел 5 — лист С13

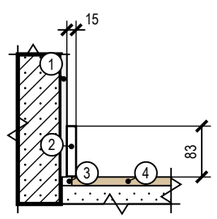

Поз.	Состав слоя, изделие
1	штукатурка, шпаклёвка Q3, окраска — по ведомости отделки
2	плинтус МДФ 83×15 под окраску в цвет стены; клей монтажный — к стене, не к полу
3	зазор покрытия у стены 8–10 мм закрывается плинтусом
4	инженерная доска дуб на клею


Примечания

1. Размеры — в мм от чистовых поверхностей стен; условные обозначения и общие указания — лист 22.

	Лист	№ док.	Подпись	Дата	Проект: Квартира 103 м²	М 1:20
Дизайнер	Кырлан А.С.			14.11.26	Развёртка стены Б. Гостиная-столовая (пом. 3)	Стадия: П; Лист: 75; Листов: 129
Проверил						
Н. контр.						
Утв.						

выпуск 14.11.2026 № 32d0256903 · стр. 75 из 129

Стена В (М 1:20)

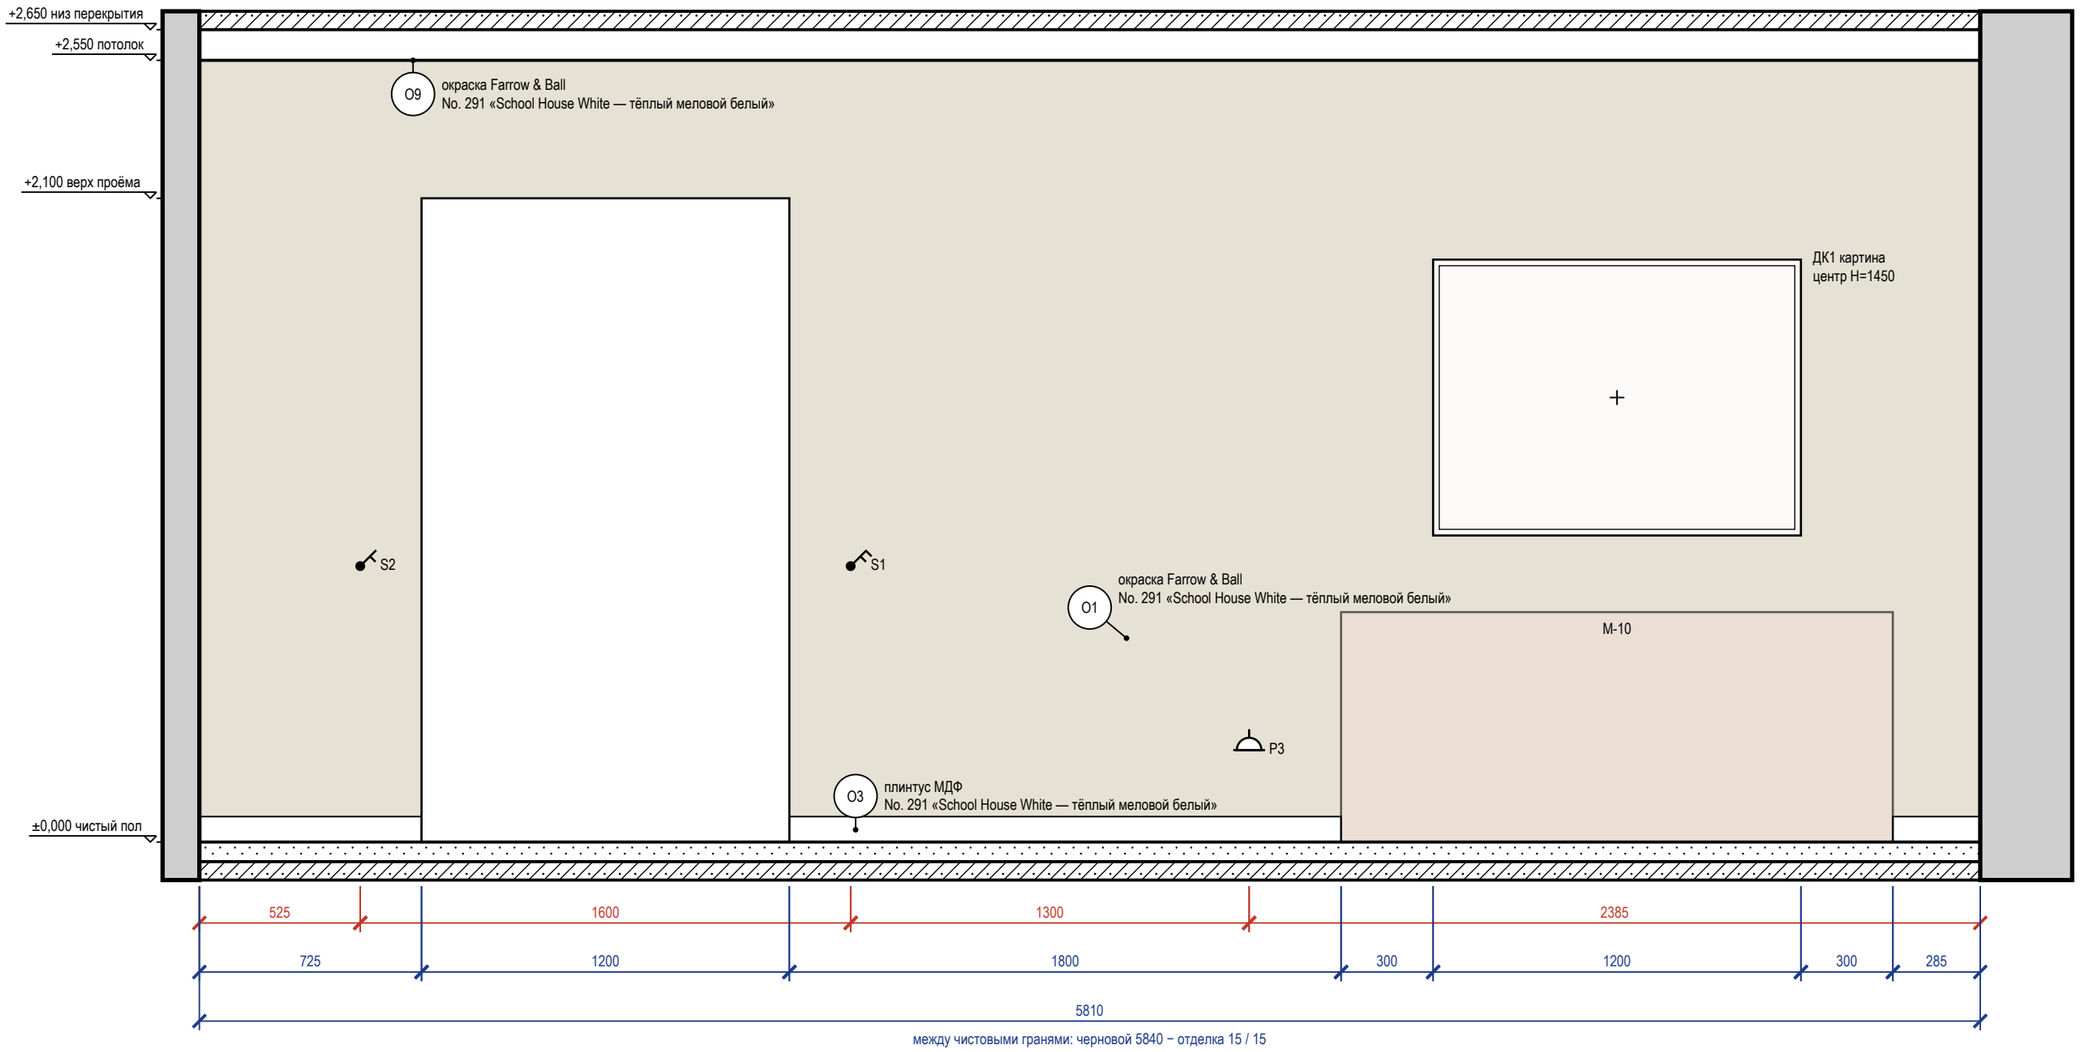


Ведомость точек и выводов

Марка	Что это	Гр.	H, мм	От угла, мм	Примечание
S2	выключатель	1	900	525	
S1	выключатель	1	900	2125	
P3	розетка: торшер у дивана M-06	5	300	3425	

Ведомость отделки (на листе)

Марка	Поверхность	Материал, изделие	Цвет, код	Кол.
O1	стены	окраска, Farrow & Ball Modern Emulsion, матовая, подготовка К3	Farrow & Ball No. 291 «School House White тёплый меловой белый»	12,3 м²
O3	плинтус	плинтус МДФ, h 83 мм, Ultrawood Base 5340, ЛДФ под окраску, 83×15 мм, 2440 мм (арт. LDF-BASE-5340), полуглянцевая	Farrow & Ball No. 291 «School House White тёплый меловой белый»	2,8 м
O9	потолок	окраска, Farrow & Ball Modern Emulsion, матовая, подготовка Q3	Farrow & Ball No. 291 «School House White тёплый меловой белый»	20,3 м²

Схема развёрток (М 1:100)

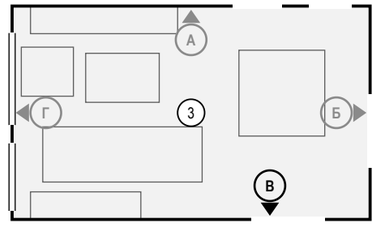


Примечания

1. Размеры — в мм от чистовых поверхностей стен; условные обозначения и общие указания — лист 22.
2. Картины и зеркала крепить к основанию по паспорту изделия (закладные и анкеры — в перечне скрытых работ); крест — ось центра предмета.

	Лист	№ док.	Подпись	Дата	Проект: Квартира 103 м²	М 1:20
Дизайнер	Кырлан А.С.			14.11.26	Развёртка стены В. Гостиная-столовая (пом. 3)	Стадия: П; Лист: 76; Листов: 129
Проверил						
Н. контр.						
Утв.						

Стена Г (М 1:20)

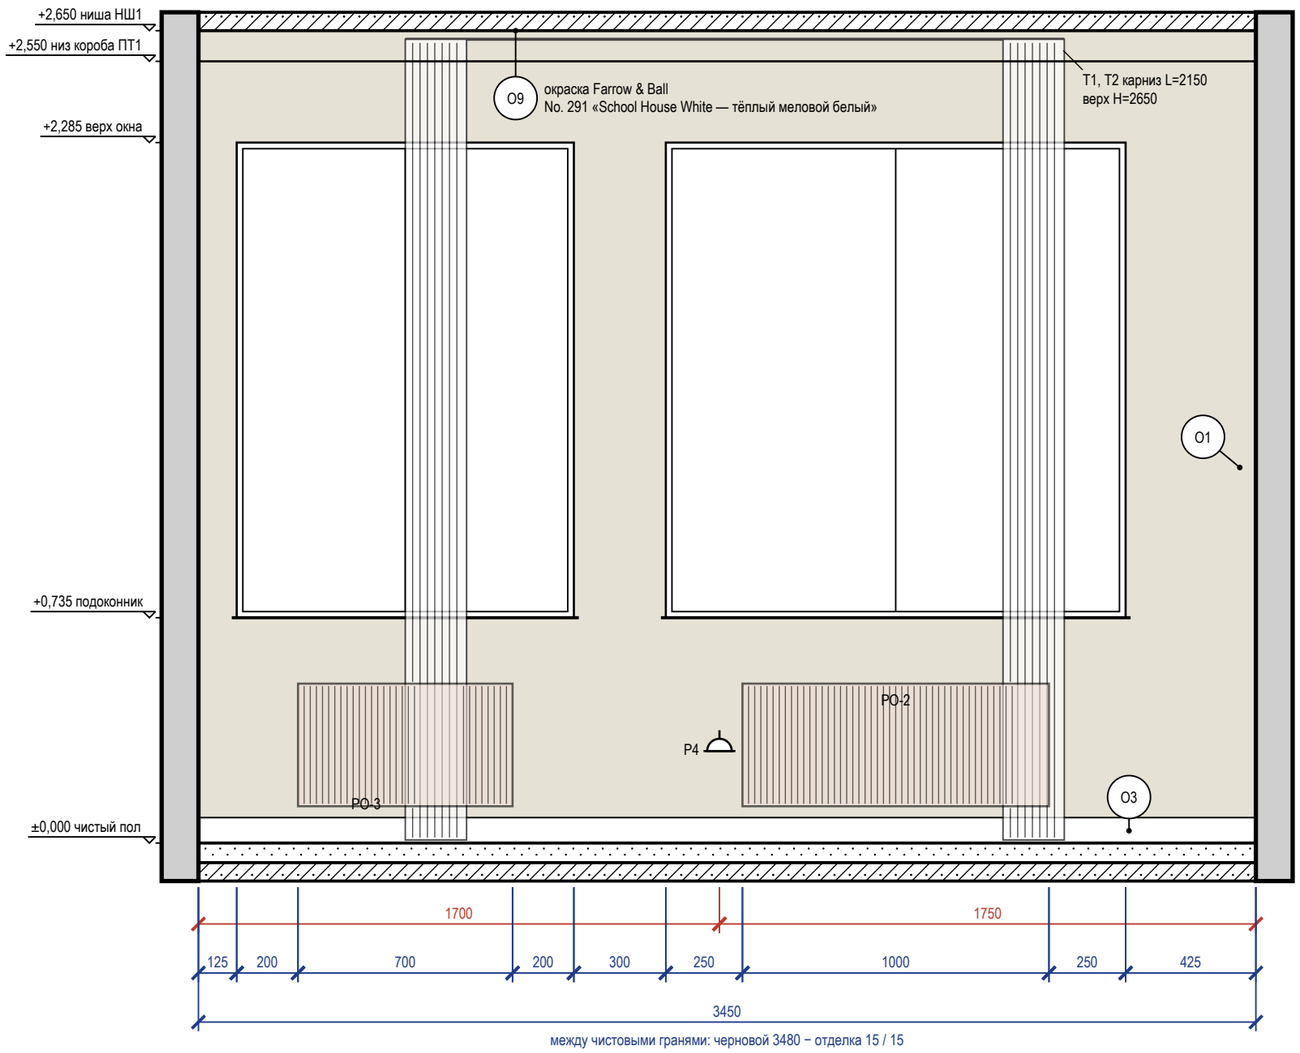

Стена Г — визуализация, лист 7


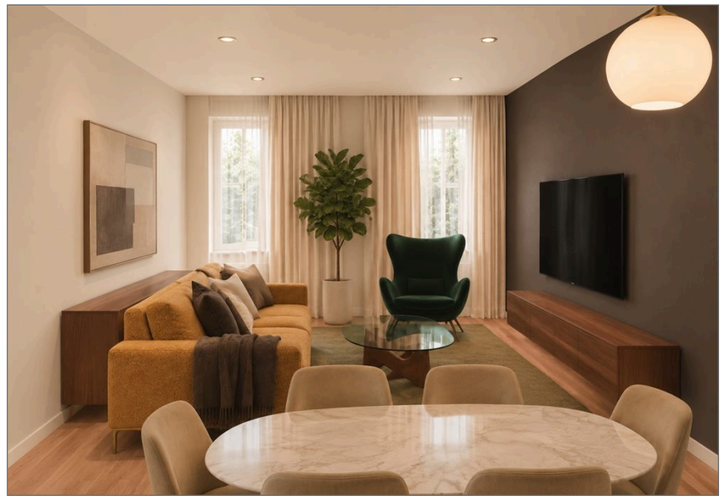


Схема развёрток (М 1:50)

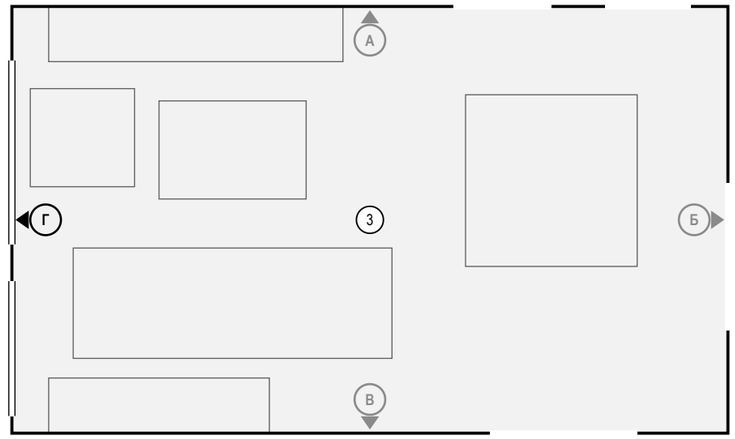

Ведомость точек и выводов

Марка	Что это	Гр.	H, мм	От угла, мм	Примечание
Р4	розетка: кресло у окна М-08	5	300	1700	

Ведомость изделий и проёмов (на листе)

Марка	Изделие, проём	На виде Ш×В, мм	Низ, мм
РО-3	радиатор отопления	700×400	120
РО-2	радиатор отопления	1000×400	120

Ведомость отделки (на листе)

Марка	Поверхность	Материал, изделие	Цвет, код	Кол.
О1	стены	окраска, Farrow & Ball Modern Emulsion, матовая, подготовка К3	Farrow & Ball No. 291 «School House White тёплый меловой белый»	5,1 м²
О3	плинтус	плинтус МДФ, h 83 мм, Ultrawood Base 5340, ЛДФ под окраску, 83×15 мм, 2440 мм (арт. LDF-BASE-5340), полуглянцевая	Farrow & Ball No. 291 «School House White тёплый меловой белый»	3,5 м
О9	потолок	окраска, Farrow & Ball Modern Emulsion, матовая, подготовка Q3	Farrow & Ball No. 291 «School House White тёплый меловой белый»	20,3 м²

Примечания

1. Размеры — в мм от чистовых поверхностей стен; условные обозначения и общие указания — лист 22.
2. Карнизы (шины) — по ведомости текстиля декоратора: длина L и верх H на развёртке — те же числа, что в ведомости; крепление — до окраски потолка.
3. Линии узора (швы плитки, складки штор, рёбра радиаторов) прерываются у знаков и выносок — просвет между линиями не менее 0,7 мм.

	Лист	№ док.	Подпись	Дата
Дизайнер	Кырлан А.С.			14.11.26
Проверил				
Н. контр.				
Утв.				


Проект: Квартира 103 м² — **М 1:20**

Развёртка стены Г.
Гостиная-столовая (пом. 3)

Стадия	Лист	Листов
П	77	129

выпуск 14.11.2026 № 32d0256903 · стр. 77 из 129


Стена А (М 1:20)

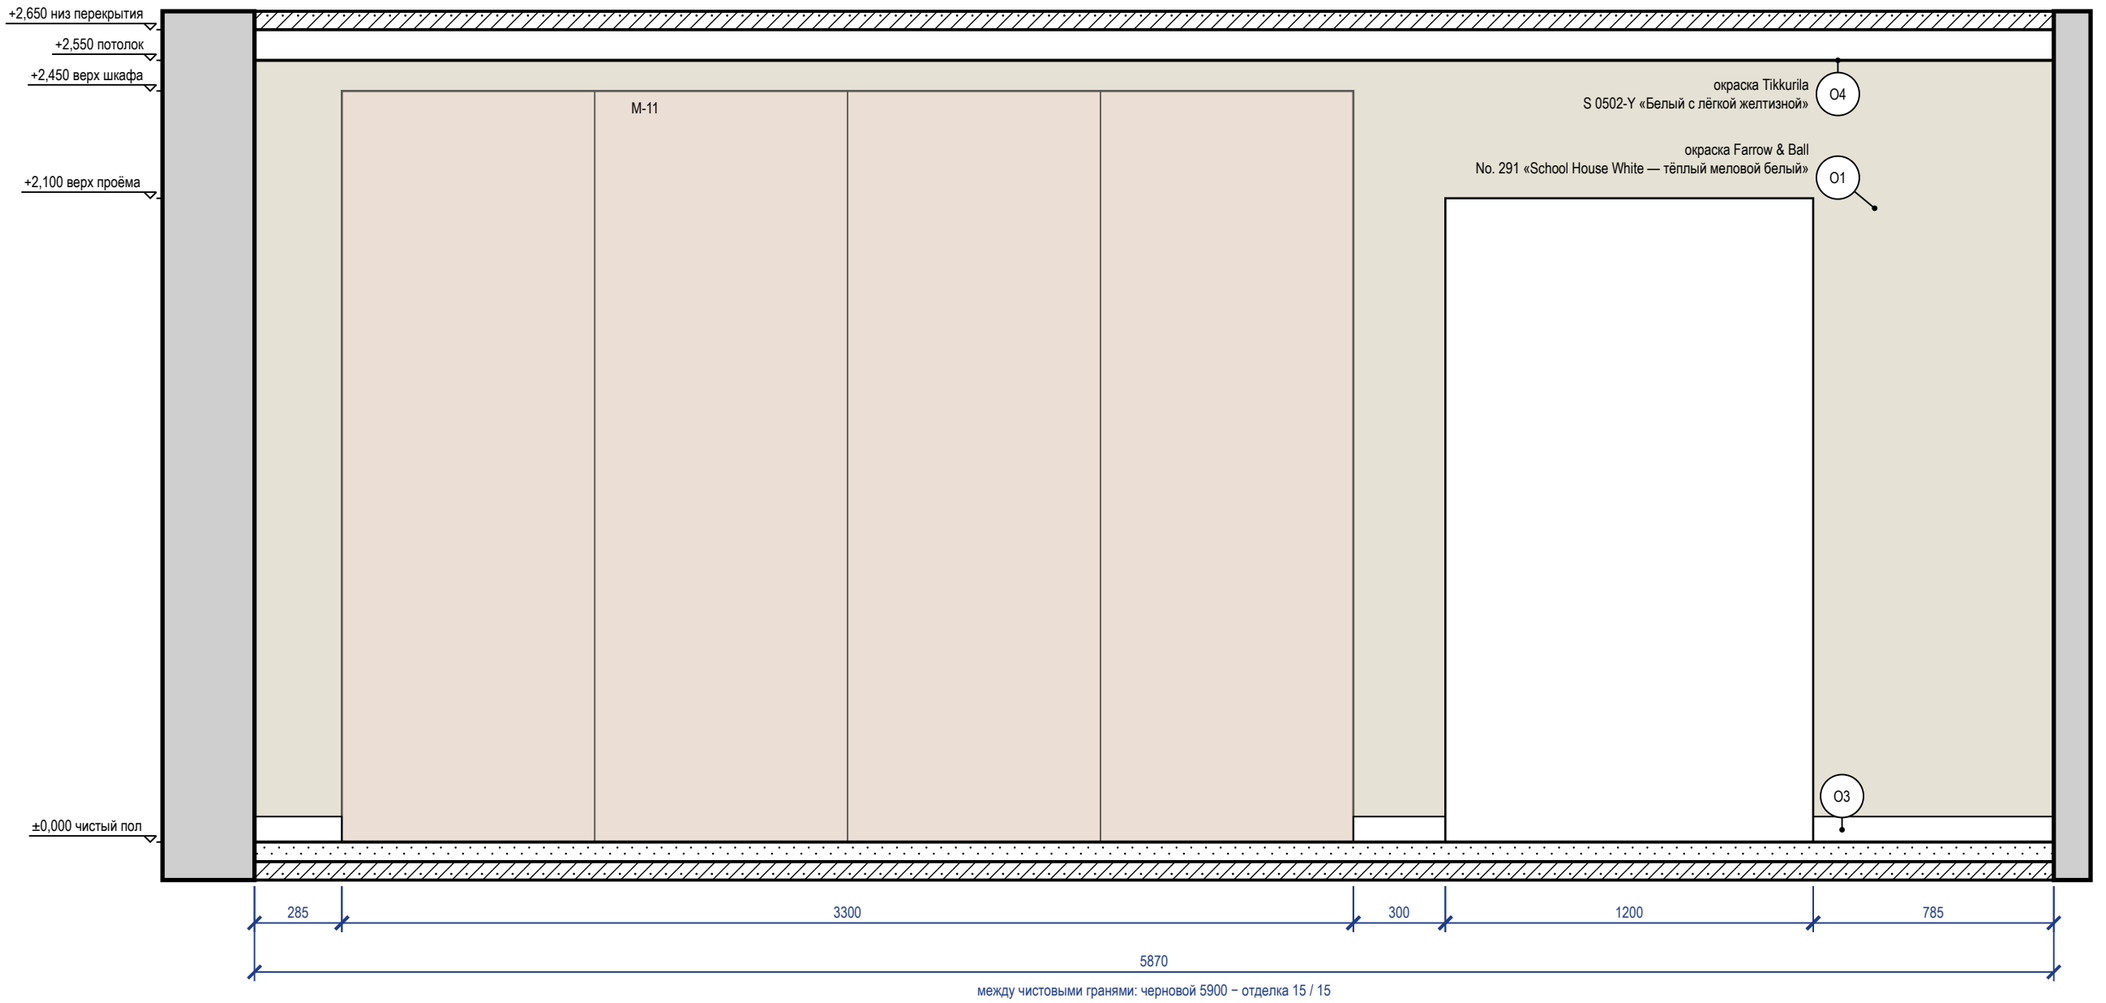

Ведомость отделки (на листе)

Марка	Поверхность	Материал, изделие	Цвет, код	Кол.
О1	стены	окраска, Farrow & Ball Modern Emulsion, матовая, подготовка Q3	Farrow & Ball No. 291 «School House White — тёплый меловой белый»	12,4 м²
О3	плинтус	плинтус МДФ, h 83 мм, Ultrawood Base 5340, ЛДФ под окраску, 83×15 мм, 2440 мм (арт. LDF-BASE-5340)	Farrow & Ball No. 291 «School House White — тёплый меловой белый»	1,4 м
О4	потолок	окраска, Tikkurila Anti-Reflex 2, глубокоматовая, подготовка Q3	NCS S 0502-Y «Белый с лёгкой желтизной»	12,9 м²

Схема развёрток (М 1:50)

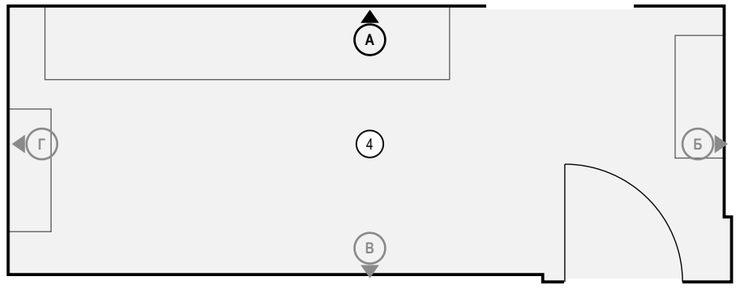

Ведомость изделий и проёмов (на листе)

Марка	Изделие, проём	На виде Ш×В, мм	Низ, мм
М-11	шкаф-купе	3300×2450	0

Примечания

1. Размеры — в мм от чистовых поверхностей стен; условные обозначения и общие указания — лист 22.

	Лист	№ док.	Подпись	Дата
Дизайнер	Кырлан А.С.			14.11.26
Проверил				
Н. контр.				
Утв.				


Проект: Квартира 103 м² — **М 1:20**

Развёртка стены А. Прихожая-холл (пом. 4)


Стадия	Лист	Листов
П	78	129

выпуск 14.11.2026 № 32d0256903 · стр. 78 из 129

Стена Б (М 1:20)

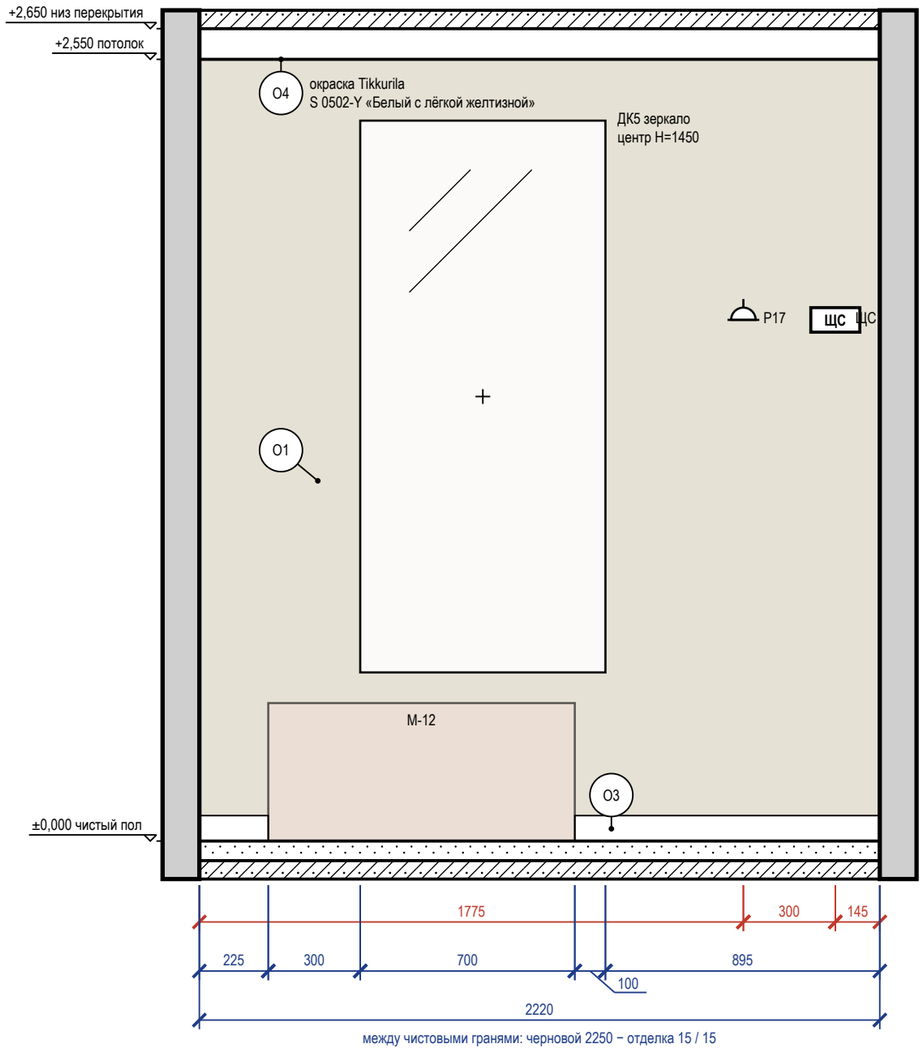

Стена Б — визуализация, лист 8

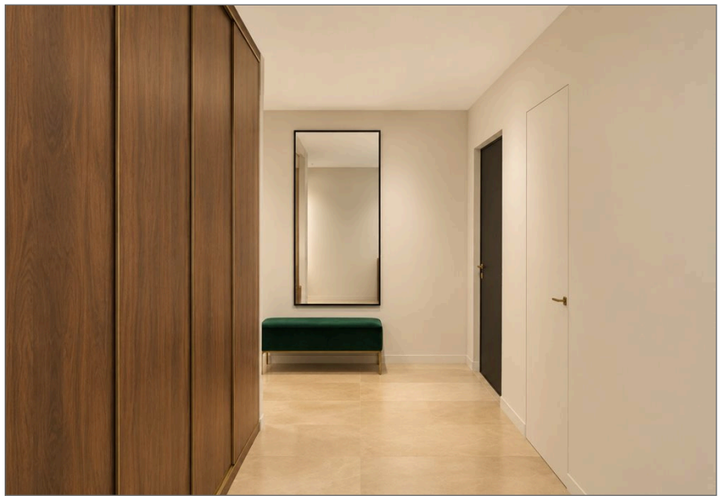


Ведомость отделки (на листе)

Марка	Поверхность	Материал, изделие	Цвет, код	Кол.
О1	стены	окраска, Farrow & Ball Modern Emulsion, матовая, подготовка Q3	Farrow & Ball No. 291 «School House White — тёплый меловой белый»	5,7 м²
О3	плинтус	плинтус МДФ, h 83 мм, Ultrawood Base 5340, ЛДФ под окраску, 83×15 мм, 2440 мм (арт. LDF-BASE-5340)	Farrow & Ball No. 291 «School House White — тёплый меловой белый»	1,2 м
О4	потолок	окраска, Tikkurila Anti-Reflex 2, глубокоматовая, подготовка Q3	NCS S 0502-Y «Белый с лёгкой желтизной»	12,9 м²

Ведомость точек и выводов

Марка	Что это	Гр.	Н, мм	От угла, мм	Примечание
Р17	розетка: питание слаботочного щита (рядом с ЩС)	14	1700	1775	
ЩС	щит: щит слаботочный: ввод оптики, ONT, роутер, патч-панель		1700	2075	

Схема развёрток (М 1:50)

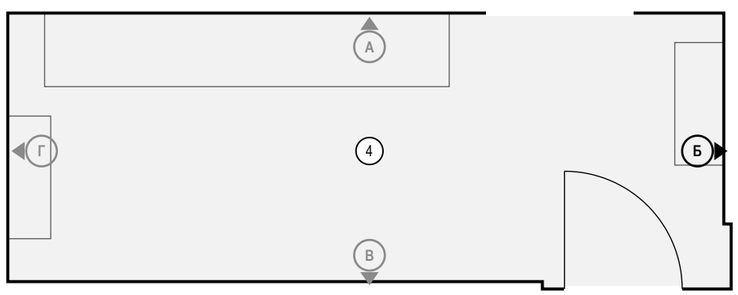

Ведомость изделий и проёмов (на листе)

Марка	Изделие, проём	На виде Ш×В, мм	Низ, мм
М-12	банкетка, изумрудный бархат, латунные ножки	1000×450	0
ДК5	зеркало	800×1800	550

Примечания

1. Размеры — в мм от чистовых поверхностей стен; условные обозначения и общие указания — лист 22.
2. Картины и зеркала крепить к основанию по паспорту изделия (закладные и анкеры — в перечне скрытых работ); крест — ось центра предмета.

	Лист	№ док.	Подпись	Дата
Дизайнер	Кырлан А.С.			14.11.26
Проверил				
Н. контр.				
Утв.				


Проект: Квартира 103 м² — **М 1:20**

Развёртка стены Б. Прихожая-холл (пом. 4)

Стадия	Лист	Листов
П	79	129

выпуск 14.11.2026 № 32d0256903 · стр. 79 из 129

Стена В (М 1:20)

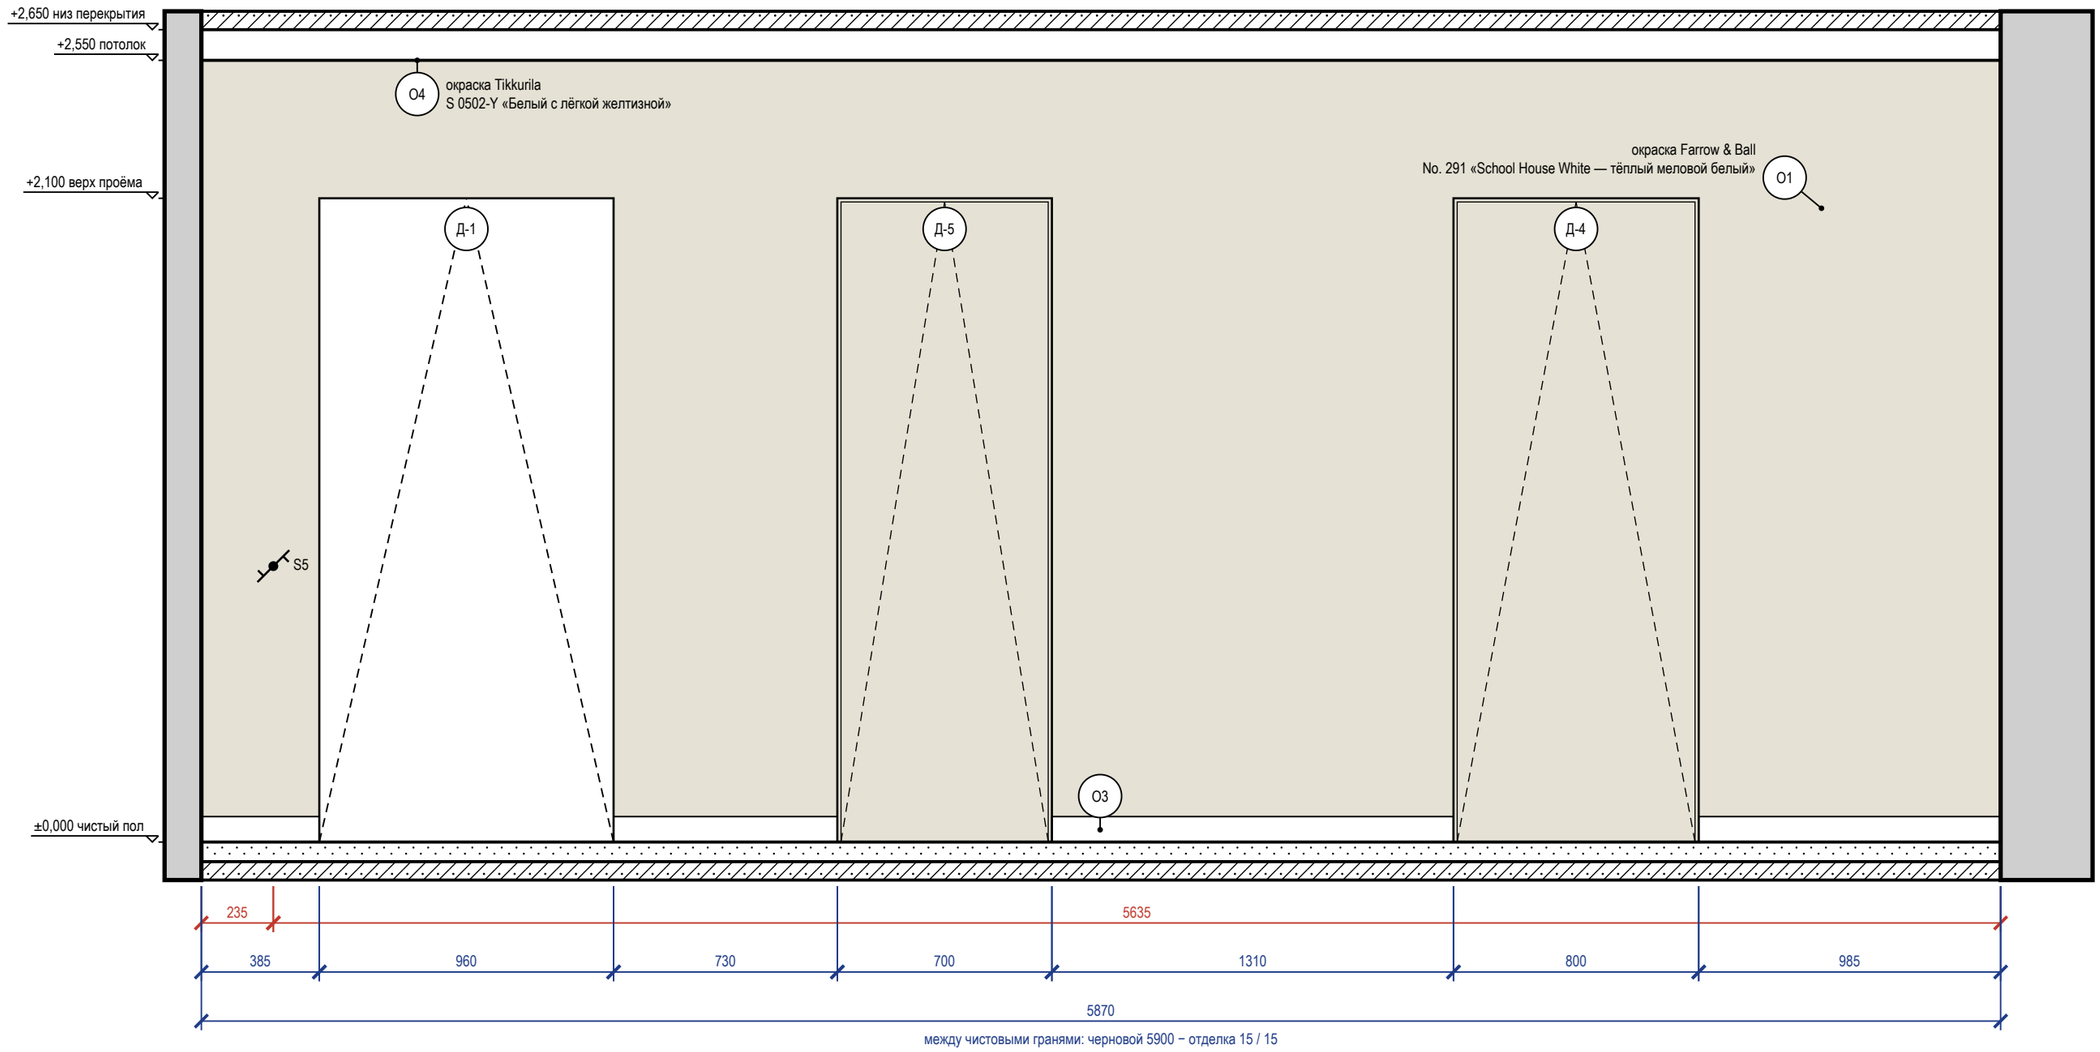

Ведомость точек и выводов

Марка	Что это	Гр.	Н, мм	От угла, мм	Примечание
S5	выключатель	2	900	235	


Ведомость изделий и проёмов (на листе)

Марка	Изделие, проём	На виде Ш×В, мм	Низ, мм
Д-1	дверь	960×2100	0
Д-5	дверь скрытого монтажа	700×2100	0
Д-4	дверь скрытого монтажа	800×2100	0

Ведомость отделки (на листе)

Марка	Поверхность	Материал, изделие	Цвет, код	Кол.
О1	стены	окраска, Farrow & Ball Modern Emulsion, матовая, подготовка Q3	Farrow & Ball No. 291 «School House White тёплый меловой белый»	9,8 м²
О3	плинтус	плинтус МДФ, h 83 мм, Ultrawood Base 5340, ЛДФ под окраску, 83×15 мм, 2440 мм (арт. LDF-BASE-5340)	Farrow & Ball No. 291 «School House White тёплый меловой белый»	3,4 м
О4	потолок	окраска, Tikkurila Anti-Reflex 2, глубокоматовая, подготовка Q3	NCS S 0502-Y «Белый с лёгкой желтизной»	12,9 м²

Схема развёрток (М 1:100)

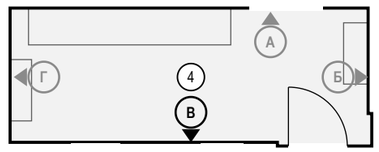


Примечания


1. Размеры — в мм от чистовых поверхностей стен; условные обозначения и общие указания — лист 22.
2. Двери скрытого монтажа — полотно в плоскости стены, отделка стены по полотну, плинтус прерывается у короба (узел — на листе узлов).

	Лист	№ док.	Подпись	Дата	Проект: Квартира 103 м²			М 1:20
Дизайнер	Кырлан А.С.			14.11.26	Развёртка стены В. Прихожая-холл (пом. 4)	Стадия	Лист	Листов
Проверил						П	80	129
Н. контр.								
Утв.								

Стена Г (М 1:20)

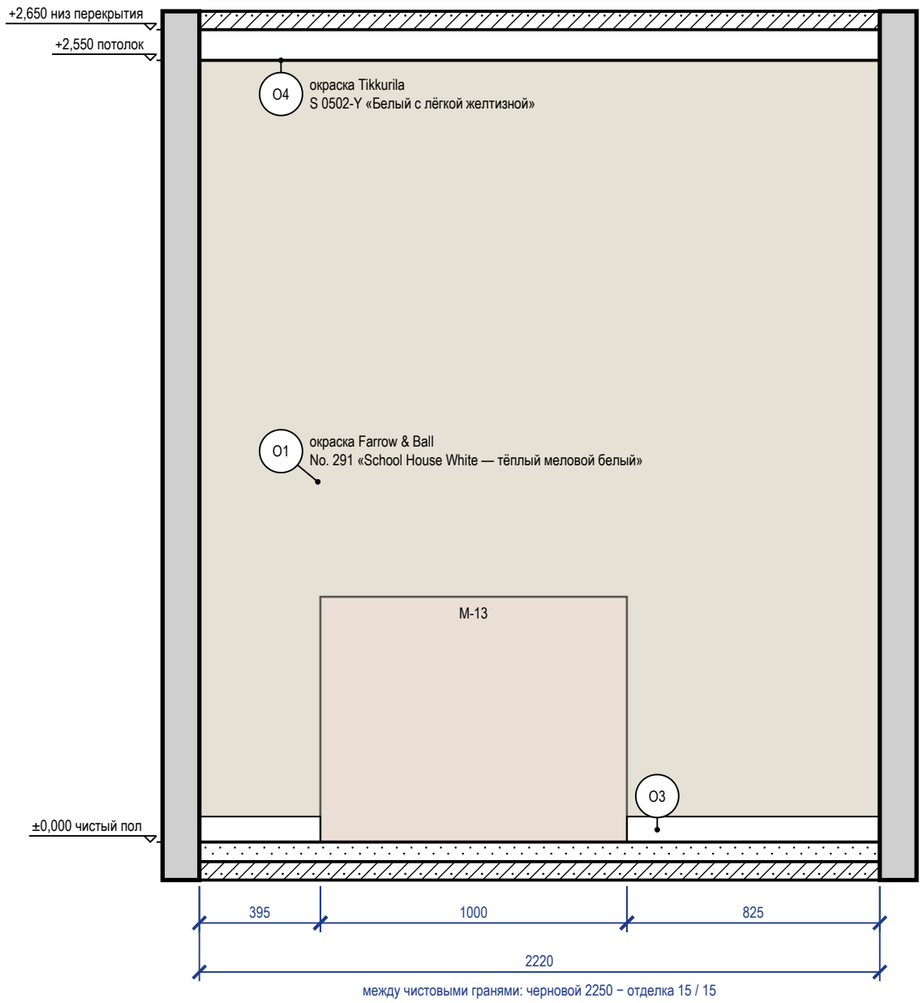

6 **Плинтус МДФ 83×15 мм у окрашенной стены по керамограниту (плитке) (М 1:5)**
Узел 6 — лист С13

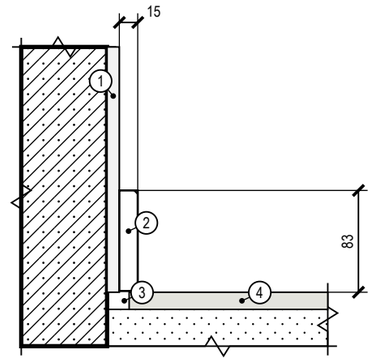


Поз.	Состав слоя, изделие
1	штукатурка, шпаклёвка Q3, окраска — по ведомости отделки
2	плинтус МДФ 83×15 под окраску в цвет стены; клей монтажный — к стене, не к полу
3	зазор покрытия у стены 8–10 мм закрывается плинтусом
4	керамогранит на клею C2 TE S1

Ведомость отделки (на листе)

Марка	Поверхность	Материал, изделие	Цвет, код	Кол.
О1	стены	окраска, Farrow & Ball Modern Emulsion, матовая, подготовка Q3	Farrow & Ball No. 291 «School House White — тёплый меловой белый»	5,7 м²
О3	плинтус	плинтус МДФ, h 83 мм, Ultrawood Base 5340, ЛДФ под окраску, 83×15 мм, 2440 мм (арт. LDF-BASE-5340)	Farrow & Ball No. 291 «School House White — тёплый меловой белый»	1,2 м
О4	потолок	окраска, Tikkurila Anti-Reflex 2, глубокоматовая, подготовка Q3	NCS S 0502-Y «Белый с лёгкой желтизной»	12,9 м²

Схема развёрток (М 1:50)

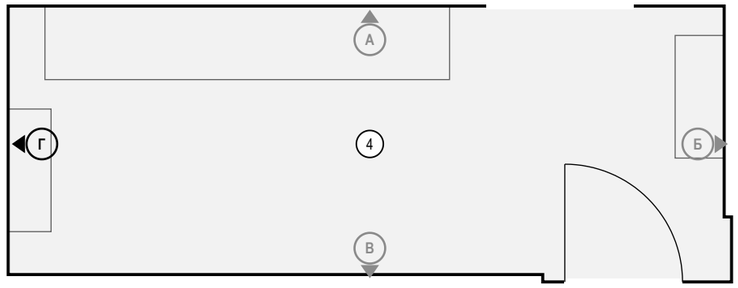

Ведомость изделий и проёмов (на листе)

Марка	Изделие, проём	На виде Ш×В, мм	Низ, мм
М-13	консоль ар-деко, чёрный лак и латунь	1000×800	0

Примечания

1. Размеры — в мм от чистовых поверхностей стен; условные обозначения и общие указания — лист 22.

	Лист	№ док.	Подпись	Дата	Проект: Квартира 103 м²			М 1:20
Дизайнер	Кырлан А.С.			14.11.26	Развёртка стены Г. Прихожая-холл (пом. 4)	Стадия	Лист	Листов
Проверил						П	81	129
Н. контр.								
Утв.								

выпуск 14.11.2026 № 32d0256903 · стр. 81 из 129

Стена Б (М 1:20)


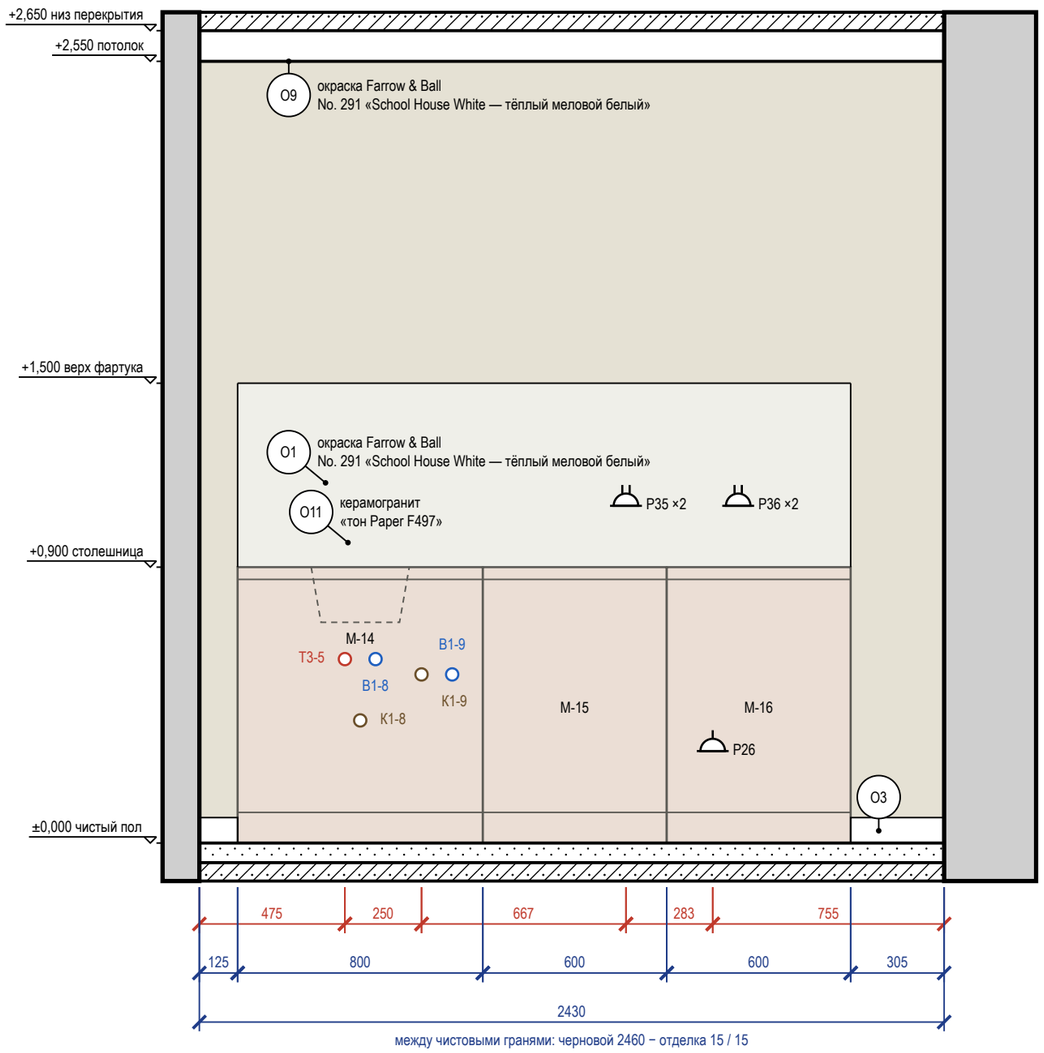


Схема развёрток (М 1:100)

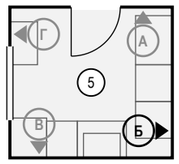

Ведомость изделий и проёмов (на листе)

Марка	Изделие, проём	На виде Ш×В, мм	Низ, мм
М-14	модуль под мойку	800×900	0
М-15	посудомоечная машина встроенная	600×900	0
М-16	модуль с ящиками	600×900	0


Примечания

1. Размеры — в мм от чистовых поверхностей стен; условные обозначения и общие указания — лист 22.
2. Выводы ВК — коды и высоты по листу выводов сантехники.
3. Выводы кухонной техники — по утверждённому проекту кухни: привязки выводов даются от осей модулей гарнитура.

Ведомость точек и выводов

Марка	Что это	Гр.	Н, мм	От угла, мм	Примечание
Т3-5	горячая вода — мойка кухонная		600	475	межос. 100
К1-8	канализация — мойка кухонная		400	525	Ø50
В1-8	холодная вода — мойка кухонная		600	575	межос. 100
К1-9	канализация — посудомоечная машина		550	725	Ø40; слив ПММ в шкафу мойки
В1-9	холодная вода — посудомоечная машина		550	825	кран ПММ в шкафу мойки
Р35	розетка: фартук	9	1100	1392	рамка 2 поста
Р26	розетка: посудомоечная машина в соседнем модуле, за ящиком	13	300	1675	
Р36	розетка: фартук	9	1100	1758	рамка 2 поста

Стена Б — визуализация, лист 9

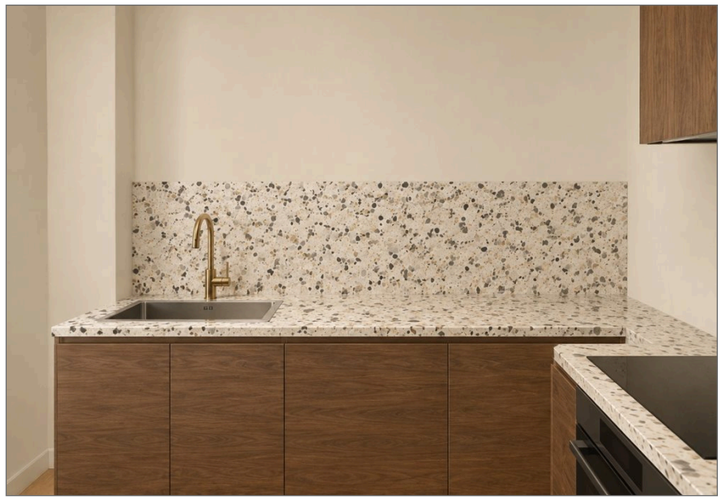


Ведомость отделки (на листе)

Марка	Поверхность	Материал, изделие	Цвет, код	Кол.
О1	стены	окраска, Farrow & Ball Modern Emulsion, матовая, подготовка К3	Farrow & Ball No. 291 «School House White — тёплый меловой белый»	5 м²
О3	плинтус	плинтус МДФ, h 83 мм, Ultrawood Base 5340, ЛДФ под окраску, 83×15 мм, 2440 мм (арт. LDF-BASE-5340), полуглянцевая	Farrow & Ball No. 291 «School House White — тёплый меловой белый»	0,4 м
О9	потолок	окраска, Farrow & Ball Modern Emulsion, матовая, подготовка Q3	Farrow & Ball No. 291 «School House White — тёплый меловой белый»	6,5 м²
О11	фартук	керамогранит, аналог: керамогранит матовый, тон F497, затирка CG2WA	#F1F1EC «тон Paper F497»	1,2 м²

	Лист	№ док.	Подпись	Дата	Проект: Квартира 103 м²	М 1:20
Дизайнер	Кырлан А.С.			14.11.26	Развёртка стены Б. Кухня (пом. 5), кухонный фронт	Стадия: П; Лист: 82; Листов: 129
Проверил						
Н. контр.						
Утв.						

выпуск 14.11.2026 № 32d0256903 · стр. 82 из 129

Стена В (М 1:20)

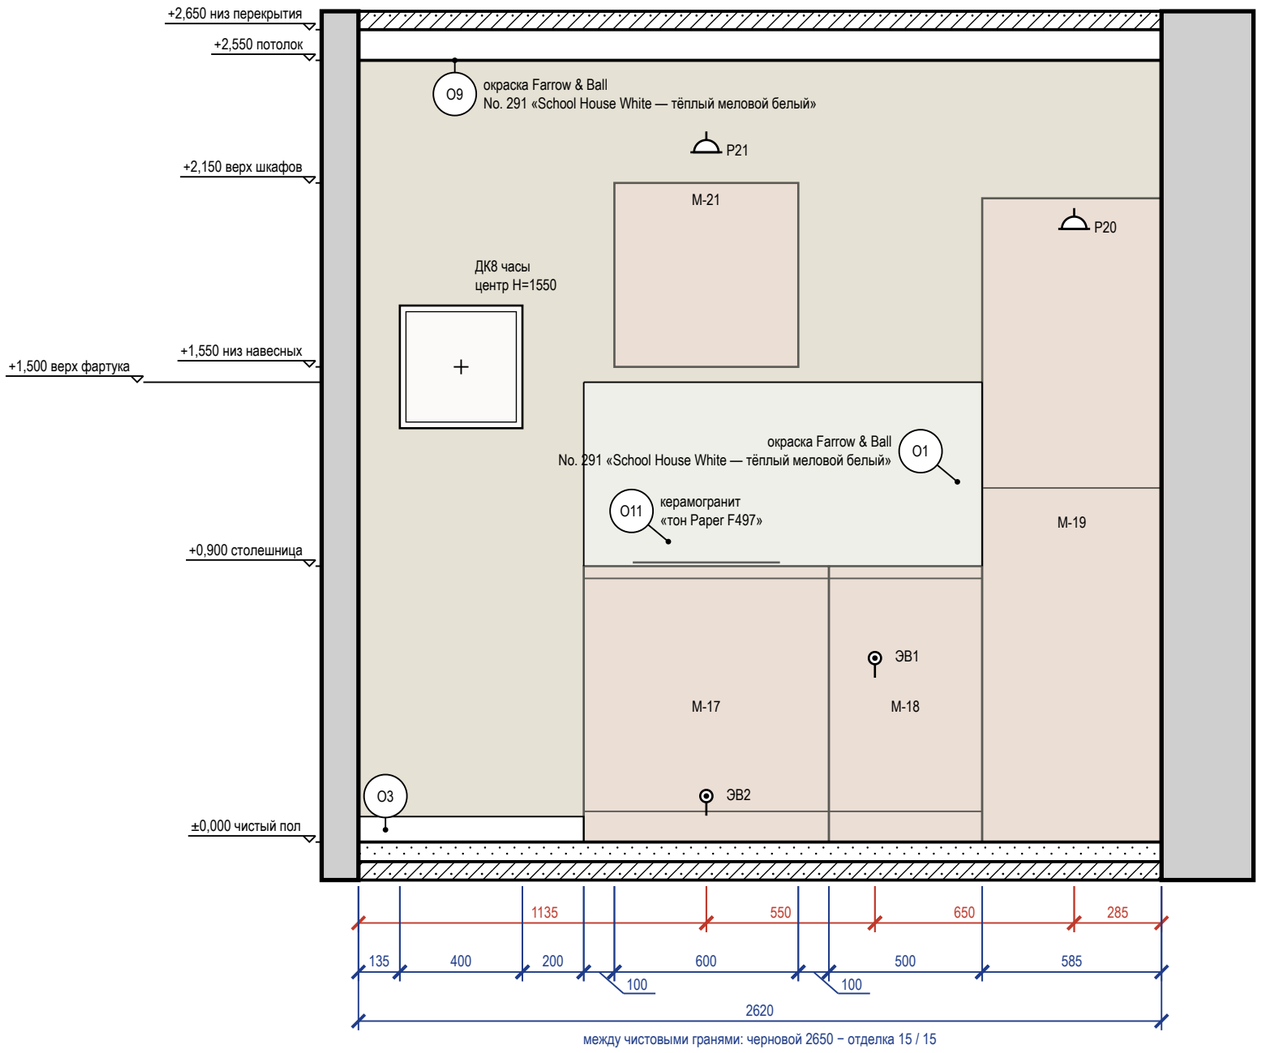

Ведомость точек и выводов

Марка	Что это	Гр.	Н, мм	От угла, мм	Примечание
ЭВ2	вывод кабеля: духовой шкаф — в цоколе	12	150	1135	
Р21	розетка: вытяжка — над корпусом	10	2250	1135	
ЭВ1	вывод кабеля: варочная панель — в соседнем модуле, за ящиком	11	600	1685	
Р20	розетка: холодильник — над нишей, съёмная панель	10	2000	2335	

Примечания

1. Размеры — в мм от чистовых поверхностей стен; условные обозначения и общие указания — лист 22.
2. Картины и зеркала крепить к основанию по паспорту изделия (закладные и анкеры — в перечне скрытых работ); крест — ось центра предмета.
3. Выводы кухонной техники — по утверждённому проекту кухни: привязки выводов даются от осей модулей гарнитура.


Стена В — визуализация, лист 10



Ведомость отделки (на листе)

Марка	Поверхность	Материал, изделие	Цвет, код	Кол.
О1	стены	окраска, Farrow & Ball Modern Emulsion, матовая, подготовка К3	Farrow & Ball No. 291 «School House White — тёплый меловой белый»	5,9 м²
О3	плинтус	плинтус МДФ, h 83 мм, Ultrawood Base 5340, ЛДФ под окраску, 83×15 мм, 2440 мм (арт. LDF-BASE-5340), полуглянцевая	Farrow & Ball No. 291 «School House White — тёплый меловой белый»	0,7 м
О9	потолок	окраска, Farrow & Ball Modern Emulsion, матовая, подготовка Q3	Farrow & Ball No. 291 «School House White — тёплый меловой белый»	6,5 м²
О11	фартук	керамогранит, аналог: керамогранит матовый, тон F497, затирка CG2WA	#F1F1EC «тон Paper F497»	0,8 м²

Схема развёрток (М 1:50)

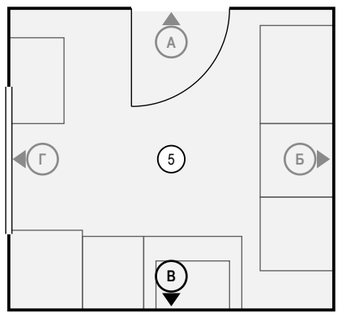

	Лист	№ док.	Подпись	Дата
Дизайнер	Кырлан А.С.			14.11.26
Проверил				
Н. контр.				
Утв.				


Проект: Квартира 103 м² — **М 1:20**

Развёртка стены В. Кухня (пом. 5), кухонный фронт

Стадия	Лист	Листов
П	83	129


выпуск 14.11.2026 № 32d0256903 · стр. 83 из 129

Стена А (М 1:20)

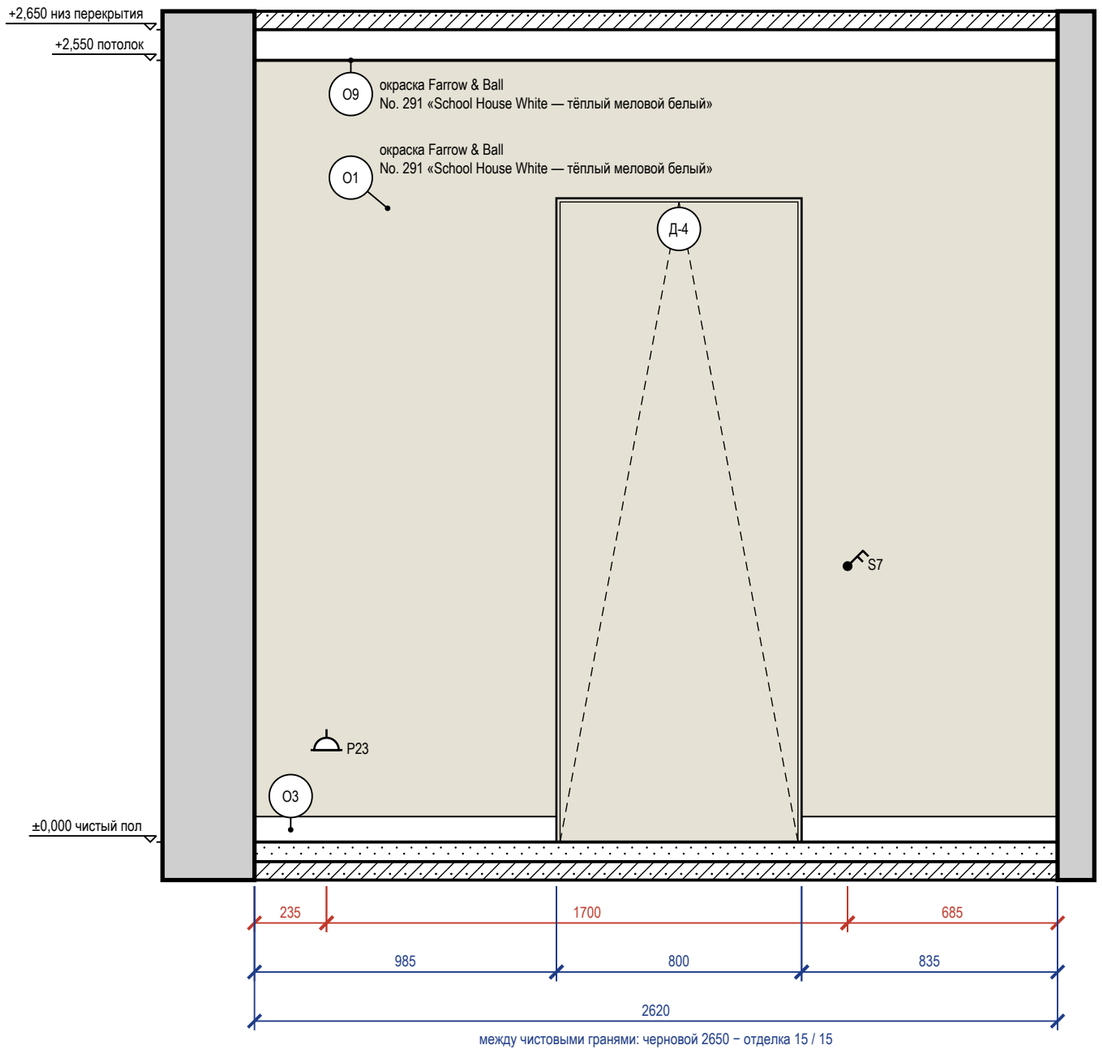

между чистовыми гранями: черновой 2650 − отделка 15 / 15

Стена Г (М 1:20)

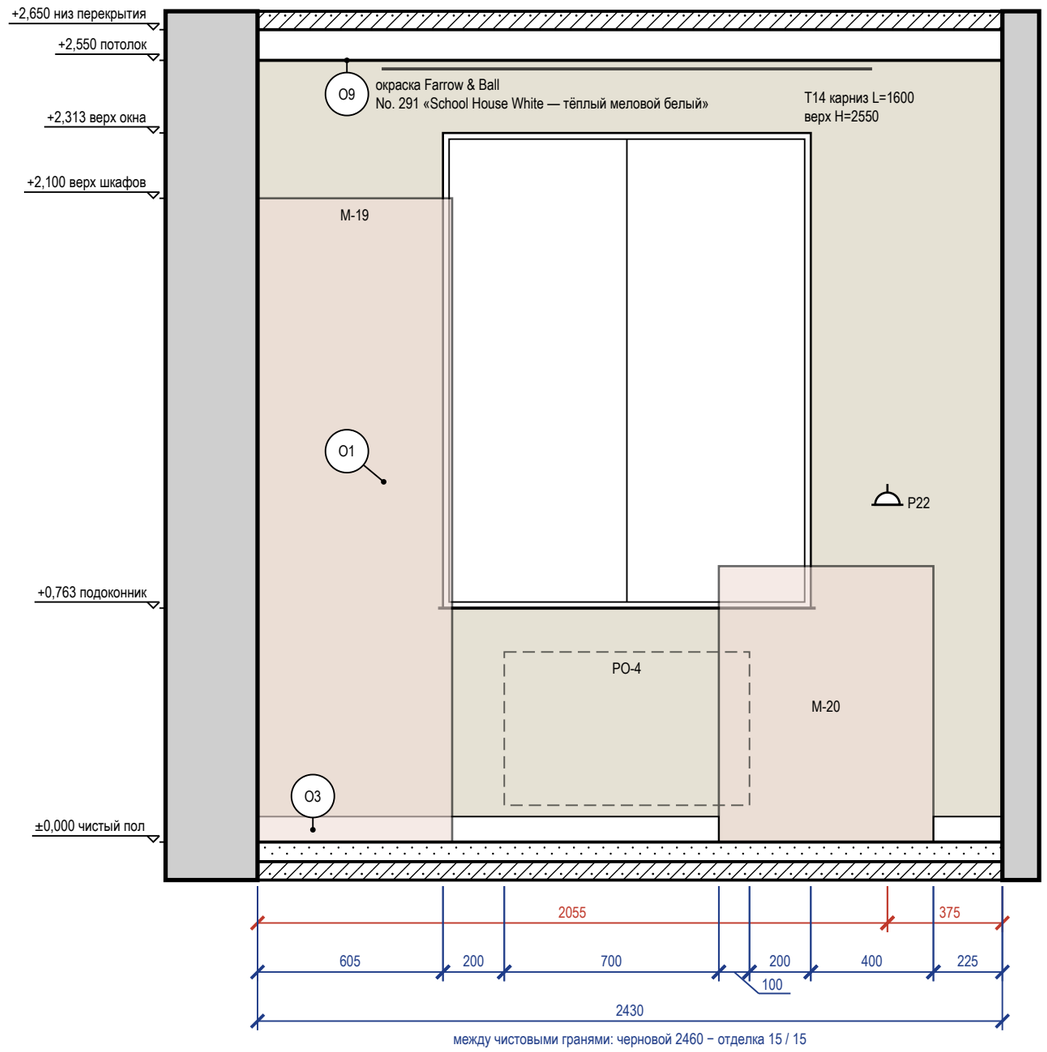

между чистовыми гранями: черновой 2460 − отделка 15 / 15


Ведомость точек и выводов

Стена	Марка	Что это	Гр.	H, мм	От угла, мм	Примечание
А	Р23	розетка: уборка	10	300	235	
А	S7	выключатель	1	900	1935	
Г	Р22	розетка: барный стол М-20: мелкая техника	10	1100	2055	

Ведомость отделки (на листе)

Марка	Поверхность	Материал, изделие	Цвет, код	Кол.
О1	стены	окраска, Farrow & Ball Modern Emulsion, матовая, подготовка К3	Farrow & Ball No. 291 «School House White тёплый меловой белый»	9,3 м²
О3	плинтус	плинтус МДФ, h 83 мм, Ultrawood Base 5340, ЛДФ под окраску, 83×15 мм, 2440 мм (арт. LDF-BASE-5340), полуглянцевая	Farrow & Ball No. 291 «School House White тёплый меловой белый»	3,5 м
О9	потолок	окраска, Farrow & Ball Modern Emulsion, матовая, подготовка Q3	Farrow & Ball No. 291 «School House White тёплый меловой белый»	6,5 м²

Схема развёрток (М 1:100)

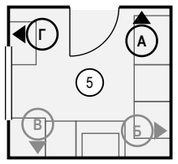

Примечания

1. Размеры — в мм от чистовых поверхностей стен; условные обозначения и общие указания — лист 22.
2. Карнизы (шины) — по ведомости текстиля декоратора: длина L и верх H на развёртке — те же числа, что в ведомости; крепление — до окраски потолка.
3. Двери скрытого монтажа — полотно в плоскости стены, отделка стены по полотну, плинтус прерывается у короба (узел — на листе узлов).

	Лист	№ док.	Подпись	Дата
Дизайнер	Кырлан А.С.			14.11.26
Проверил				
Н. контр.				
Утв.				


Проект: Квартира 103 м² — **М 1:20**

Развёртки стен А, Г. Кухня (пом. 5)


Стадия	Лист	Листов
П	84	129

выпуск 14.11.2026 № 32d0256903 · стр. 84 из 129

Стена А (М 1:20)

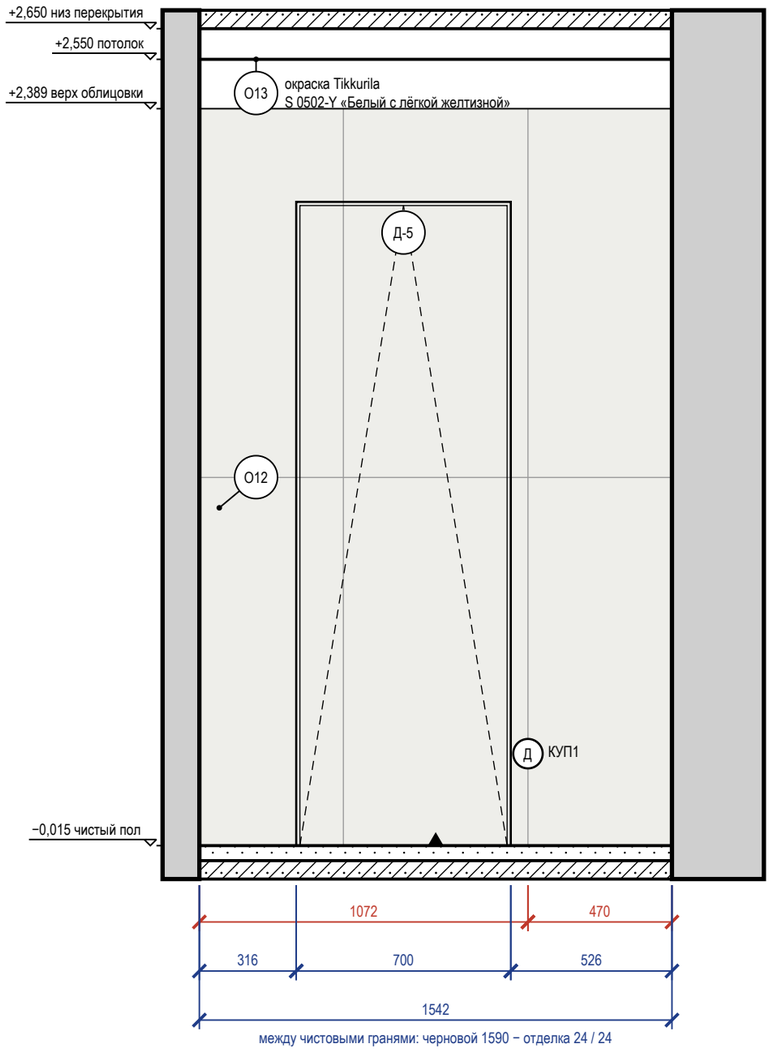

Стена В (М 1:20)

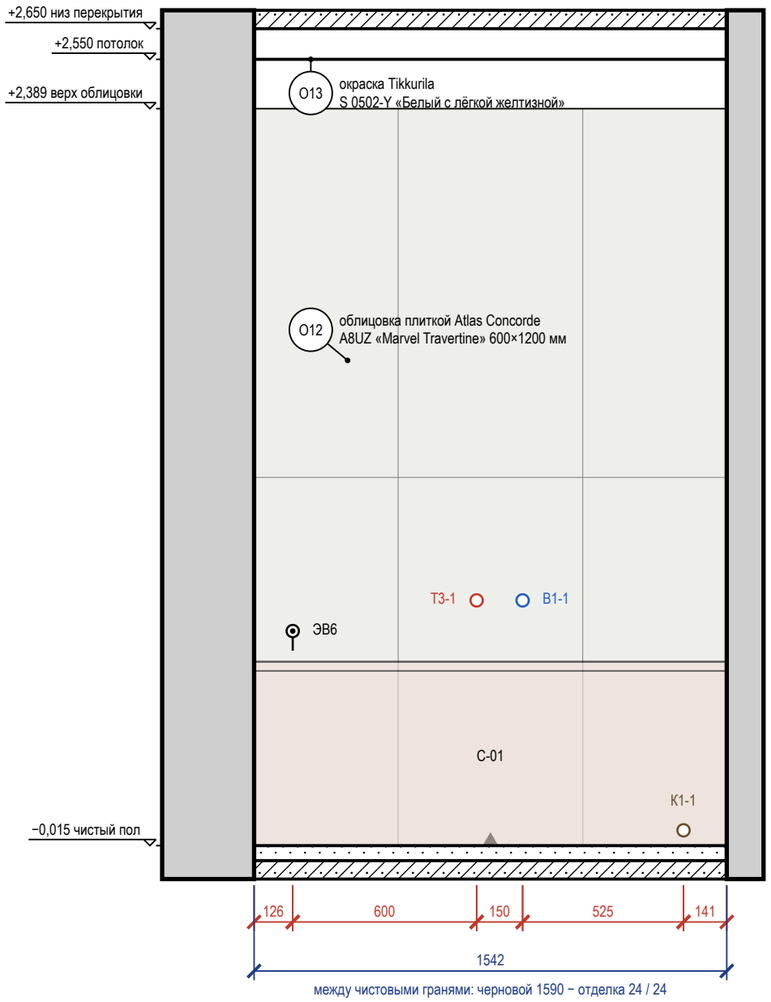

Стена В — визуализация, лист 12


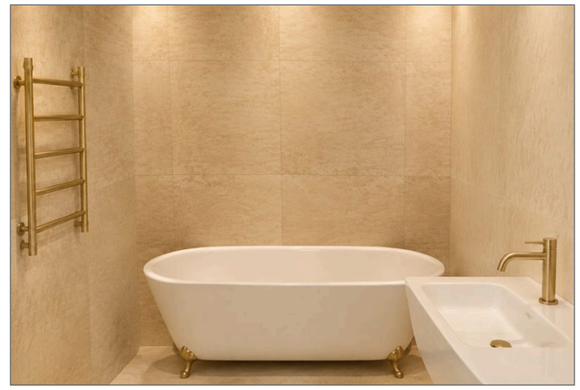


Схема развёрток (М 1:50)

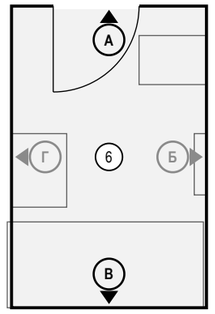

Ведомость точек и выводов

Стена	Марка	Что это	Гр.	Н, мм	От угла, мм	Примечание
А	КУП1	КУП (уравнивание потенциалов): КУП уравнивание потенциалов (ДСУП)		300	1072	
В	ЭВ6	вывод кабеля: полотенцесушитель П10	7	700	126	
В	Т3-1	горячая вода — ванна		800	726	межос. 150
В	В1-1	холодная вода — ванна		800	876	межос. 150
В	К1-1	канализация — ванна		50	1401	Ø50

Ведомость отделки (на листе)

Марка	Поверхность	Материал, изделие	Цвет, код	Кол.
О12	стены	облицовка плиткой, Atlas Concorde Marvel Travertine, 600×1200×9 мм, A8UZ, затирка CG2WA	Atlas Concorde A8UZ «Marvel Travertine»	5,9 м²
О13	потолок	окраска, Tikkurila Luja 7, матовая, подготовка Q3	NCS S 0502-Y «Белый с лёгкой желтизной»	3,9 м²

Ведомость изделий и проёмов (на листе)

Стена	Марка	Изделие, проём	На виде Ш×В, мм	Низ, мм
А	Д-5	дверь скрытого монтажа	700×2100	0
В	С-01	ванна отдельностоящая на латунных лапах 1600×700	1541×600	0

Примечания

1. Размеры — в мм от чистовых поверхностей стен; условные обозначения и общие указания — лист 22.
2. Схема мебели, приборов и декора не является технической документацией для производства мебели; габариты — по паспортам изделий.
3. Выводы ВК — коды и высоты по листу выводов сантехники.
4. Облицовка — по сетке швов 2 мм, раскладка от оси стены (треугольник у пола), целые ряды от пола; подрезки — по листу раскладки плитки.
5. Гидроизоляция в 2 слоя, заход на стены 200 мм; над ванной — до 2000 и 300 мм за борт — до облицовки, с актом скрытых работ и тестом проливом (узел — на листе узлов).
6. Двери скрытого монтажа — полотно в плоскости стены, отделка стены по полотну, плинтус прерывается у короба (узел — на листе узлов).

	Лист	№ док.	Подпись	Дата
Дизайнер	Кырлан А.С.			14.11.26
Проверил				
Н. контр.				
Утв.				


Проект: Квартира 103 м² — М 1:20

Развёртки стен А, В. Ванная (пом. 6)

Стадия	Лист	Листов
П	85	129

выпуск 14.11.2026 № 32d0256903 · стр. 85 из 129


Стена Б (М 1:20)

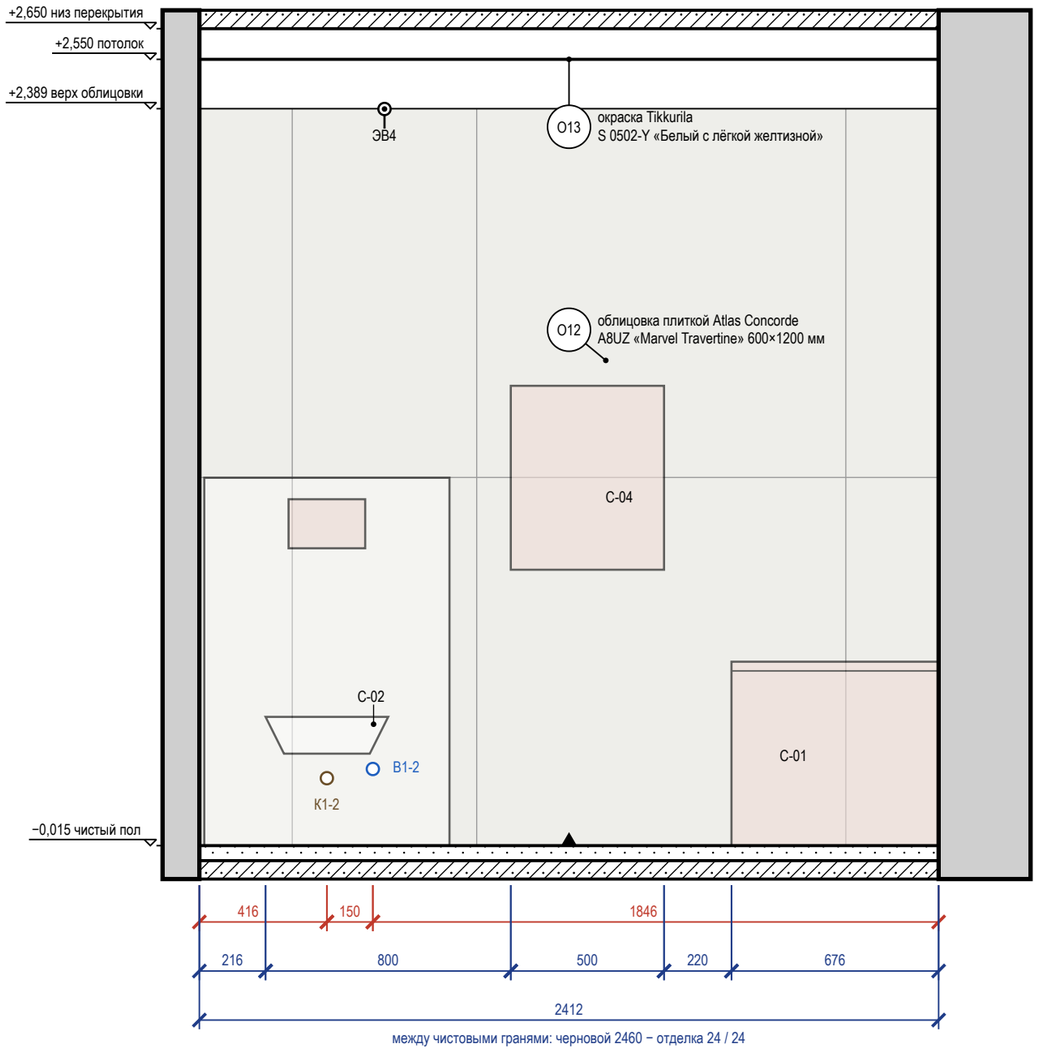

Стена Б — визуализация, лист 11



Схема развёрток (М 1:50)

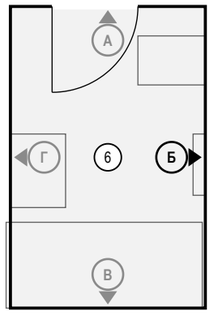

Ведомость точек и выводов

Марка	Что это	Гр.	Н, мм	От угла, мм	Примечание
К1-2	канализация — унитаз подвесной		220	416	Ø110
В1-2	холодная вода — унитаз подвесной		250	566	в раме инсталляции
ЭВ4	вывод кабеля: вентилятор ВР1 (таймер выбега)	3	2403	604	

Ведомость отделки (на листе)

Марка	Поверхность	Материал, изделие	Цвет, код	Кол.
О12	стены	облицовка плиткой, Atlas Concorde Marvel Travertine, 600×1200×9 мм, A8UZ, затирка CG2WA	Atlas Concorde A8UZ «Marvel Travertine»	5,8 м²
О13	потолок	окраска, Tikkurila Luja 7, матовая, подготовка Q3	NCS S 0502-Y «Белый с лёгкой желтизной»	3,9 м²

Ведомость изделий и проёмов (на листе)

Марка	Изделие, проём	На виде Ш×В, мм	Низ, мм
С-02	унитаз подвесной	400×120	300
С-04	полотенцесушитель электрический, латунный цвет	500×600	900
С-01	ванна отдельностоящая на латунных лапах 1600×700	676×600	0

Примечания

1. Размеры — в мм от чистовых поверхностей стен; условные обозначения и общие указания — лист 22.
2. Схема мебели, приборов и декора не является технической документацией для производства мебели; габариты — по паспортам изделий.
3. Выводы ВК — коды и высоты по листу выводов сантехники.
4. Облицовка — по сетке швов 2 мм, раскладка от оси стены (треугольник у пола), целые ряды от пола; подрезки — по листу раскладки плитки.
5. Гидроизоляция в 2 слоя, заход на стены 200 мм; над ванной — до 2000 и 300 мм за борт — до облицовки, с актом скрытых работ и тестом проливом (узел — на листе узлов).

	Лист	№ док.	Подпись	Дата
Дизайнер	Кырлан А.С.			14.11.26
Проверил				
Н. контр.				
Утв.				

Проект: Квартира 103 м² — **М 1:20**

Развёртка стены Б. Ванная (пом. 6)

Стадия	Лист	Листов
П	86	129

выпуск 14.11.2026 № 32d0256903 · стр. 86 из 129

Стена Г (М 1:20)


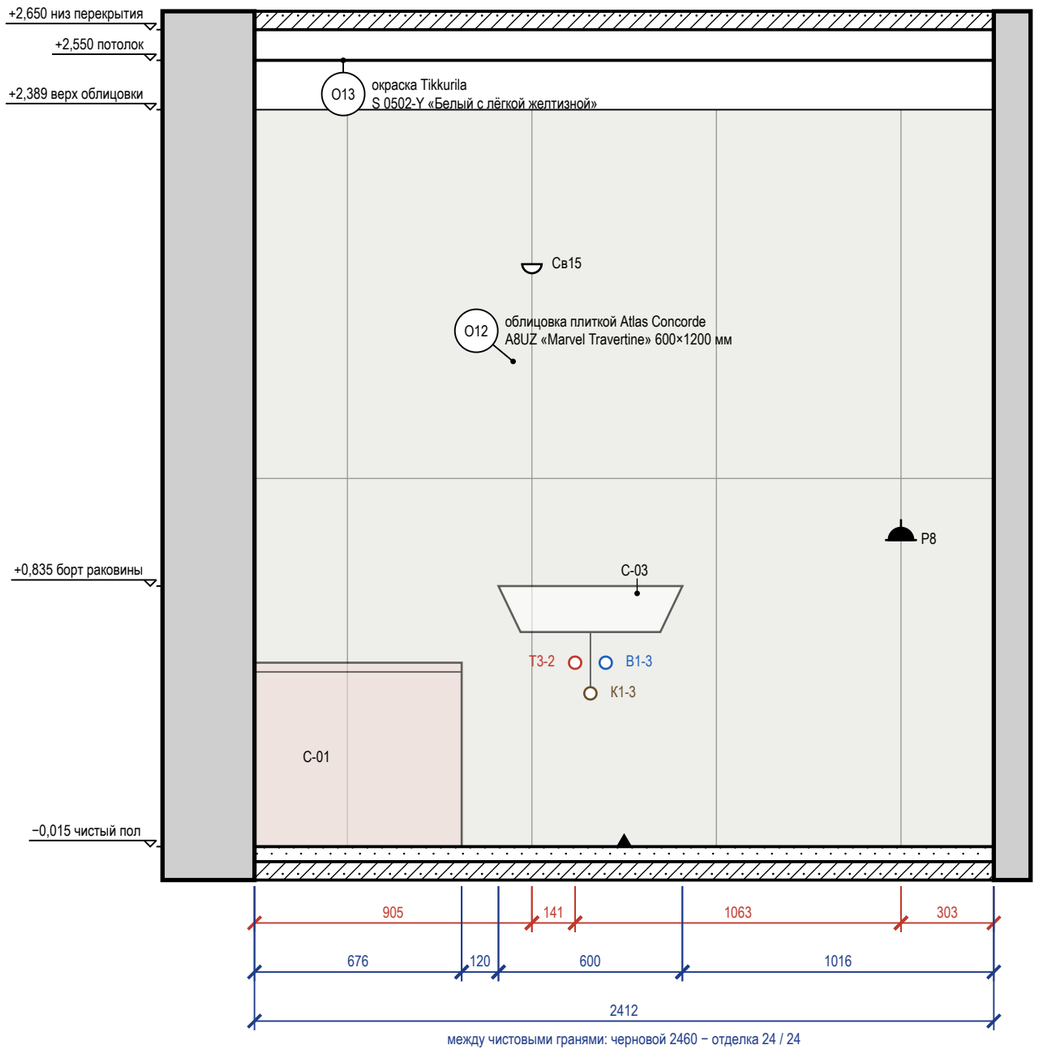


Схема развёрток (М 1:50)

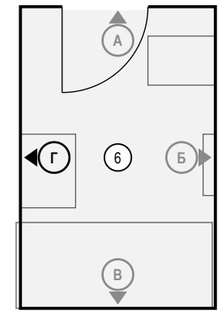

Ведомость точек и выводов

Марка	Что это	Гр.	Н, мм	От угла, мм	Примечание
Св15	светильник настенный	3	1900	905	
Т3-2	горячая вода — умывальник		600	1046	межос. 100
К1-3	канализация — умывальник		500	1096	Ø50
В1-3	холодная вода — умывальник		600	1146	межос. 100
Р8	розетка: фен у умывальника	7	1000	2109	IP44

Ведомость отделки (на листе)

Марка	Поверхность	Материал, изделие	Цвет, код	Кол.
О12	стены	облицовка плиткой, Atlas Concorde Marvel Travertine, 600×1200×9 мм, A8UZ, затирка CG2WA	Atlas Concorde A8UZ «Marvel Travertine»	5,8 м²
О13	потолок	окраска, Tikkurila Luja 7, матовая, подготовка Q3	NCS S 0502-Y «Белый с лёгкой желтизной»	3,9 м²

Ведомость изделий и проёмов (на листе)

Марка	Изделие, проём	На виде Ш×В, мм	Низ, мм
С-01	ванна отдельностоящая на латунных лапах 1600×700	676×600	0
С-03	раковина на консоли ар-деко, латунь	600×150	700

Примечания

1. Размеры — в мм от чистовых поверхностей стен; условные обозначения и общие указания — лист 22.
2. Схема мебели, приборов и декора не является технической документацией для производства мебели; габариты — по паспортам изделий.
3. Выводы ВК — коды и высоты по листу выводов сантехники.
4. Облицовка — по сетке швов 2 мм, раскладка от оси стены (треугольник у пола), целые ряды от пола; подрезки — по листу раскладки плитки.
5. Гидроизоляция в 2 слоя, заход на стены 200 мм; над ванной — до 2000 и 300 мм за борт — до облицовки, с актом скрытых работ и тестом проливом (узел — на листе узлов).

	Лист	№ док.	Подпись	Дата
Дизайнер	Кырлан А.С.			14.11.26
Проверил				
Н. контр.				
Утв.				


Проект: Квартира 103 м² — **М 1:20**

Развёртка стены Г. Ванная (пом. 6)

Стадия	Лист	Листов
П	87	129


выпуск 14.11.2026 № 32d0256903 · стр. 87 из 129

Стена А (М 1:20)

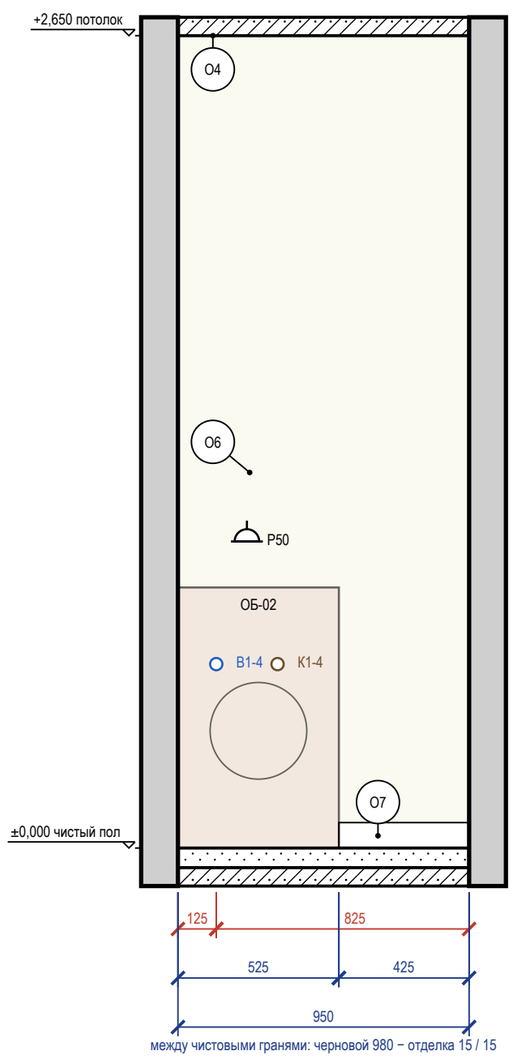


между чистовыми гранями: черновой 980 − отделка 15 / 15

Стена Б (М 1:20)

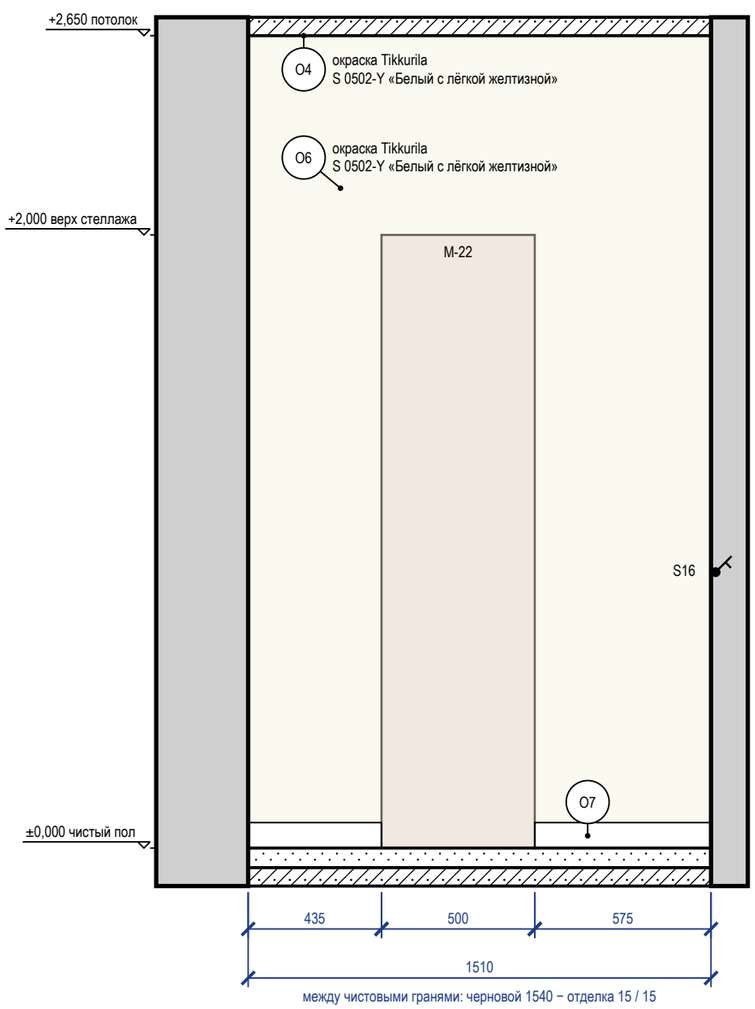

между чистовыми гранями: черновой 1540 − отделка 15 / 15

Стена Б — визуализация, лист 13

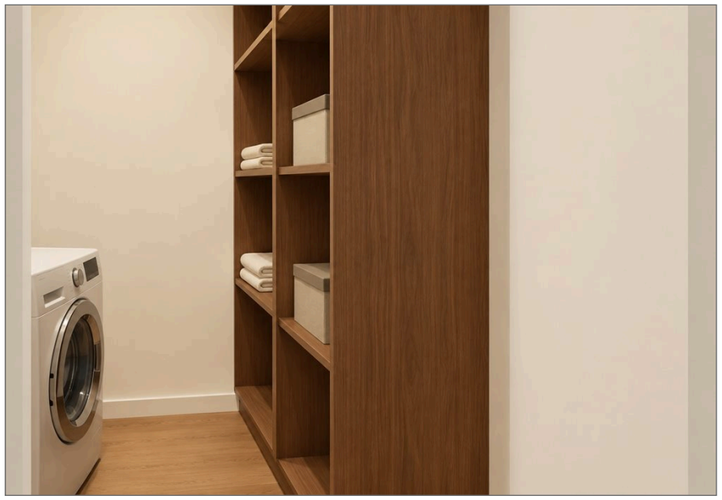


Ведомость отделки (на листе)

Марка	Поверхность	Материал, изделие	Цвет, код	Кол.
О4	потолок	окраска, Tikkurila Anti-Reflex 2, глубокоматовая, подготовка Q3	NCS S 0502-Y «Белый с лёгкой желтизной»	1,5 м²
О6	стены	окраска, Tikkurila Harmony, матовая, подготовка Q3	NCS S 0502-Y «Белый с лёгкой желтизной»	6,5 м²
О7	плинтус	плинтус МДФ, h 83 мм, Ultrawood Base 5340, ЛДФ под окраску, 83×15 мм, 2440 мм (арт. LDF-BASE-5340)	NCS S 0502-Y «Белый с лёгкой желтизной»	1,4 м

Ведомость точек и выводов

Стена	Марка	Что это	Гр.	Н, мм	От угла, мм	Примечание
А	В1-4	холодная вода — стиральная машина		600	125	кран машины
А	Р50	розетка: стиральная машина	8	1000	225	
А	К1-4	канализация — стиральная машина		600	325	Ø50
Б	S16	выключатель	1	900	1525	

Схема развёрток (М 1:50)

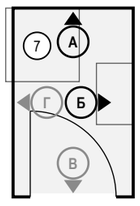

Ведомость изделий и проёмов (на листе)

Стена	Марка	Изделие, проём	На виде Ш×В, мм	Низ, мм
А	ОБ-02	стиральная машина, сушильная машина в колонне	525×850	0
Б	М-22	полки для хранения (стена Б, в стороне от короба стояков)	500×2000	0

Примечания

1. Размеры — в мм от чистовых поверхностей стен; условные обозначения и общие указания — лист 22.
2. Схема мебели, приборов и декора не является технической документацией для производства мебели; габариты — по паспортам изделий.
3. Выводы ВК — коды и высоты по листу выводов сантехники.

	Лист	№ док.	Подпись	Дата
Дизайнер	Кырлан А.С.			14.11.26
Проверил				
Н. контр.				
Утв.				


Проект: Квартира 103 м² — М 1:20

Развёртки стен А, Б. Постирочная (пом. 7)

Стадия	Лист	Листов
П	88	129


выпуск 14.11.2026 № 32d0256903 · стр. 88 из 129

Стена В (М 1:20)

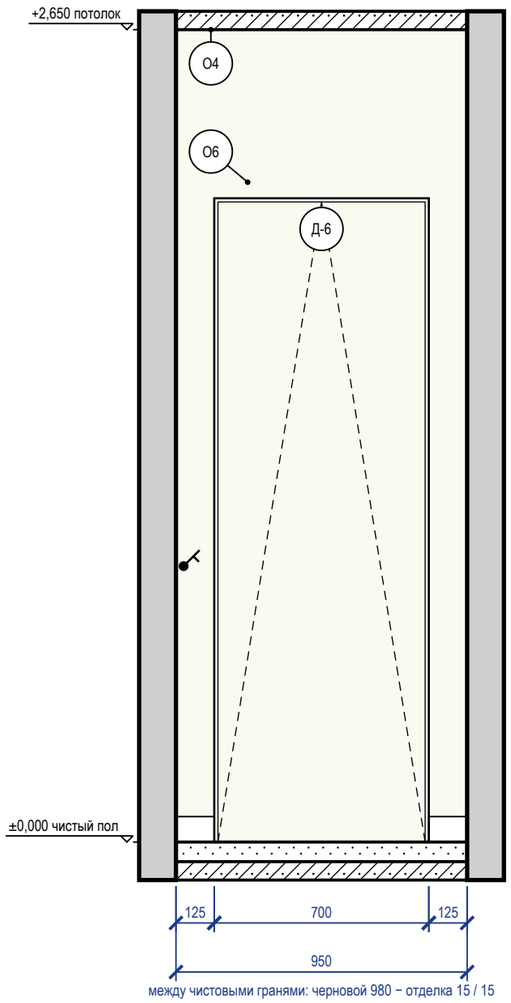

между чистовыми гранями: черновой 980 − отделка 15 / 15


Стена Г (М 1:20)

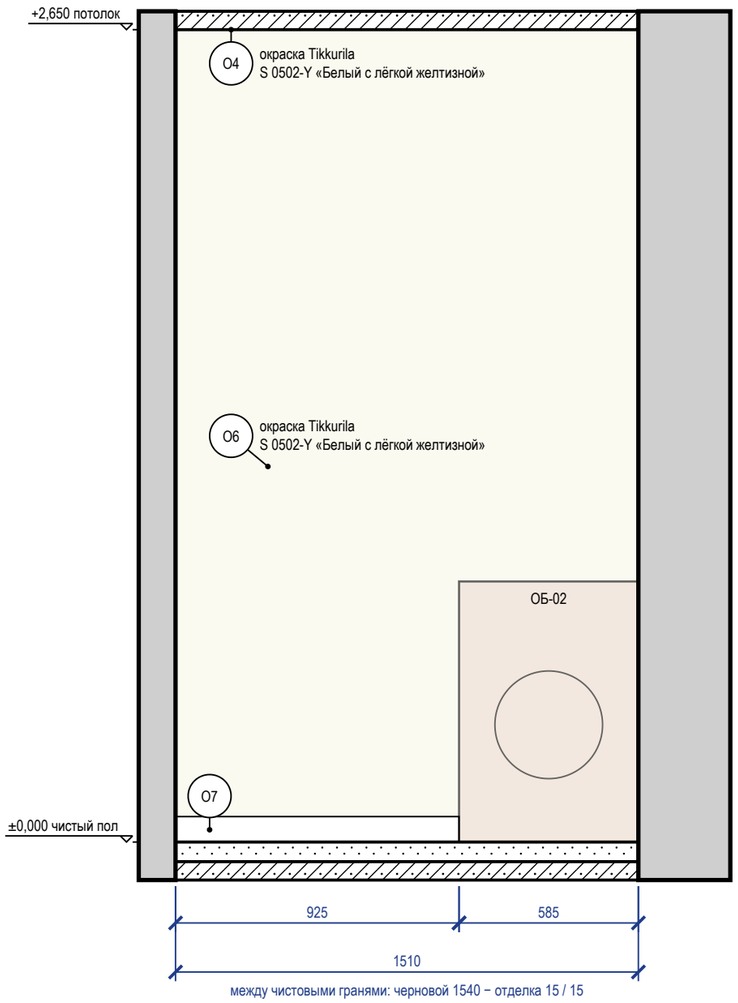

между чистовыми гранями: черновой 1540 − отделка 15 / 15

2 Дверь скрытого монтажа в плоскости стены, плинтус (М 1:5)


Узел 2 — лист С13

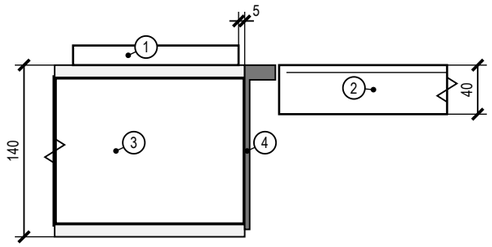

Поз.	Состав слоя, изделие
1	плинтус МДФ 83×16 на клей; у короба — зазор 5 мм, окраска в цвет стены
2	полотно 40 мм под окраску, заподлицо со стеной; теневой шов 3 мм
3	стена 120 мм, штукатурка 10 мм с двух сторон
4	короб скрытого монтажа (алюминий), лицом в плоскости отделки; монтаж до штукатурки

5 Плинтус МДФ 83×15 мм у окрашенной стены по доске (ламинату) (М 1:5)

Узел 5 — лист С13

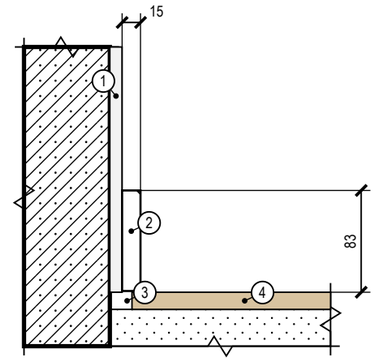

Поз.	Состав слоя, изделие
1	штукатурка, шпаклёвка Q3, окраска — по ведомости отделки
2	плинтус МДФ 83×15 под окраску в цвет стены; клей монтажный — к стене, не к полу
3	зазор покрытия у стены 8–10 мм закрывается плинтусом
4	инженерная доска дуб на клею

Ведомость точек и выводов

Стена	Марка	Что это	Гр.	Н, мм	От угла, мм	Примечание
В	S16	выключатель	1	900	25	


Ведомость изделий и проёмов (на листе)

Стена	Марка	Изделие, проём	На виде Ш×В, мм	Низ, мм
В	Д-6	дверь скрытого монтажа	700×2100	0
Г	ОБ-02	стиральная машина, сушильная машина в колонне	585×850	0

Ведомость отделки (на листе)

Марка	Поверхность	Материал, изделие	Цвет, код	Кол.
О4	потолок	окраска, Tikkurila Anti-Reflex 2, глубокоматовая, подготовка Q3	NCS S 0502-Y «Белый с лёгкой желтизной»	1,5 м²
О6	стены	окраска, Tikkurila Harmony, матовая, подготовка Q3	NCS S 0502-Y «Белый с лёгкой желтизной»	5 м²
О7	плинтус	плинтус МДФ, h 83 мм, Ultrawood Base 5340, ЛДФ под окраску, 83×15 мм, 2440 мм (арт. LDF-BASE-5340)	NCS S 0502-Y «Белый с лёгкой желтизной»	1,2 м

Схема развёрток (М 1:50)

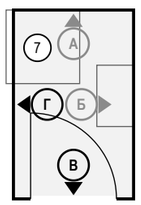


Примечания

1. Размеры — в мм от чистовых поверхностей стен; условные обозначения и общие указания — лист 22.
2. Схема мебели, приборов и декора не является технической документацией для производства мебели; габариты — по паспортам изделий.
3. Двери скрытого монтажа — полотно в плоскости стены, отделка стены по полотну, плинтус прерывается у короба (узел — на листе узлов).
4. Часть марок не уместилась у знаков: коды, высоты и привязки этих позиций — в ведомости точек и выводов под видами.


	Лист	№ док.	Подпись	Дата	Проект: Квартира 103 м²			М 1:20
Дизайнер	Кырлан А.С.			14.11.26	Развёртки стен В, Г. Постирочная (пом. 7)	Стадия	Лист	Листов
Проверил						П	89	129
Н. контр.								
Утв.								

выпуск 14.11.2026 № 32d0256903 · стр. 89 из 129

Стена А (М 1:20)

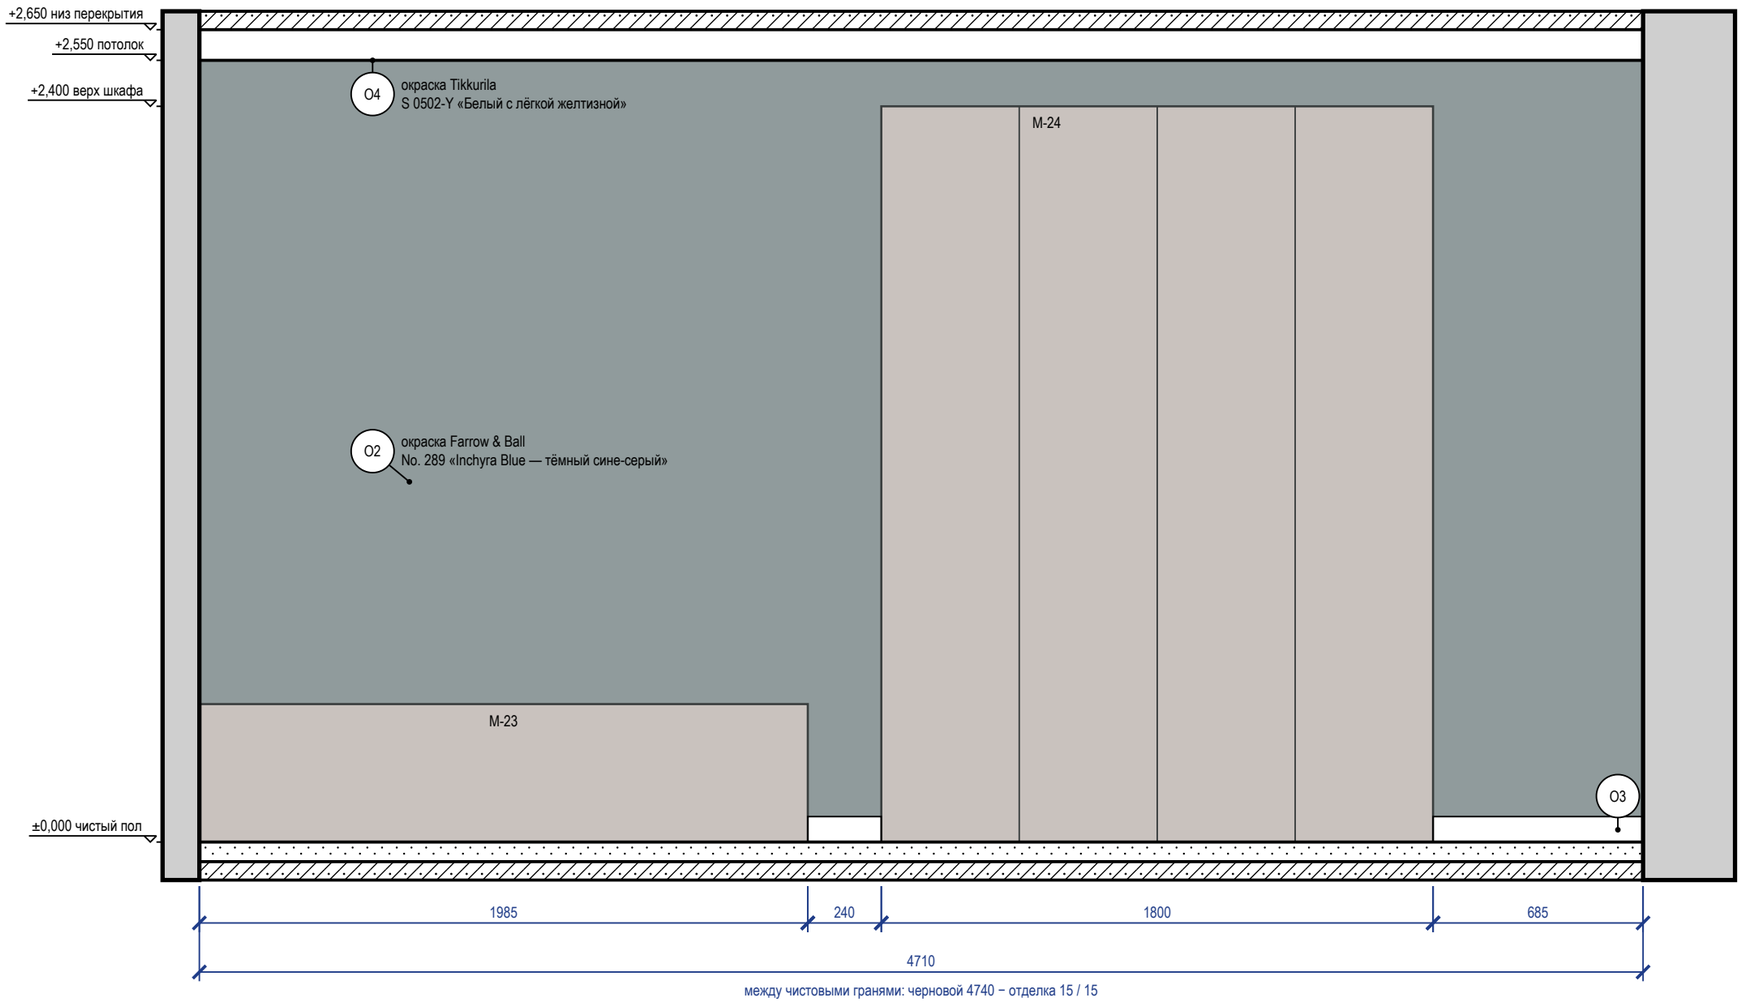


Стена А — визуализация, лист 14

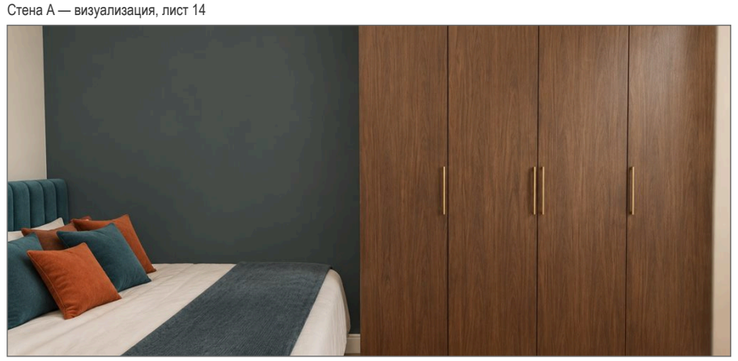

Ведомость отделки (на листе)

Марка	Поверхность	Материал, изделие	Цвет, код	Кол.
О2	акцентная стена	окраска, Farrow & Ball Modern Emulsion, матовая, подготовка Q3	Farrow & Ball No. 289 «Inchyra Blue — тёмный сине-серый»	12 м²
О3	плинтус	плинтус МДФ, h 83 мм, Ultrawood Base 5340, ЛДФ под окраску, 83×15 мм, 2440 мм (арт. LDF-BASE-5340)	Farrow & Ball No. 291 «School House White — тёплый меловой белый»	0,9 м
О4	потолок	окраска, Tikkurila Anti-Reflex 2, глубокоматовая, подготовка Q3	NCS S 0502-Y «Белый с лёгкой желтизной»	11,4 м²

Схема развёрток (М 1:50)

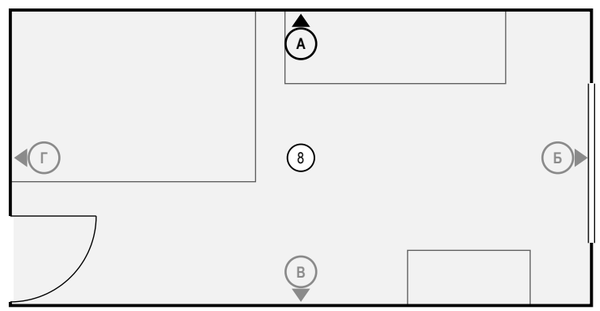


Примечания

1. Размеры — в мм от чистовых поверхностей стен; условные обозначения и общие указания — лист 22.

	Лист	№ док.	Подпись	Дата	Проект: Квартира 103 м²	М 1:20		
Дизайнер	Кырлан А.С.			14.11.26	Развёртка стены А. Спальня 2 (пом. 8)	Стадия	Лист	Листов
Проверил						П	90	129
Н. контр.								
Утв.								

выпуск 14.11.2026 № 32d0256903 · стр. 90 из 129

Стена Б (М 1:20)

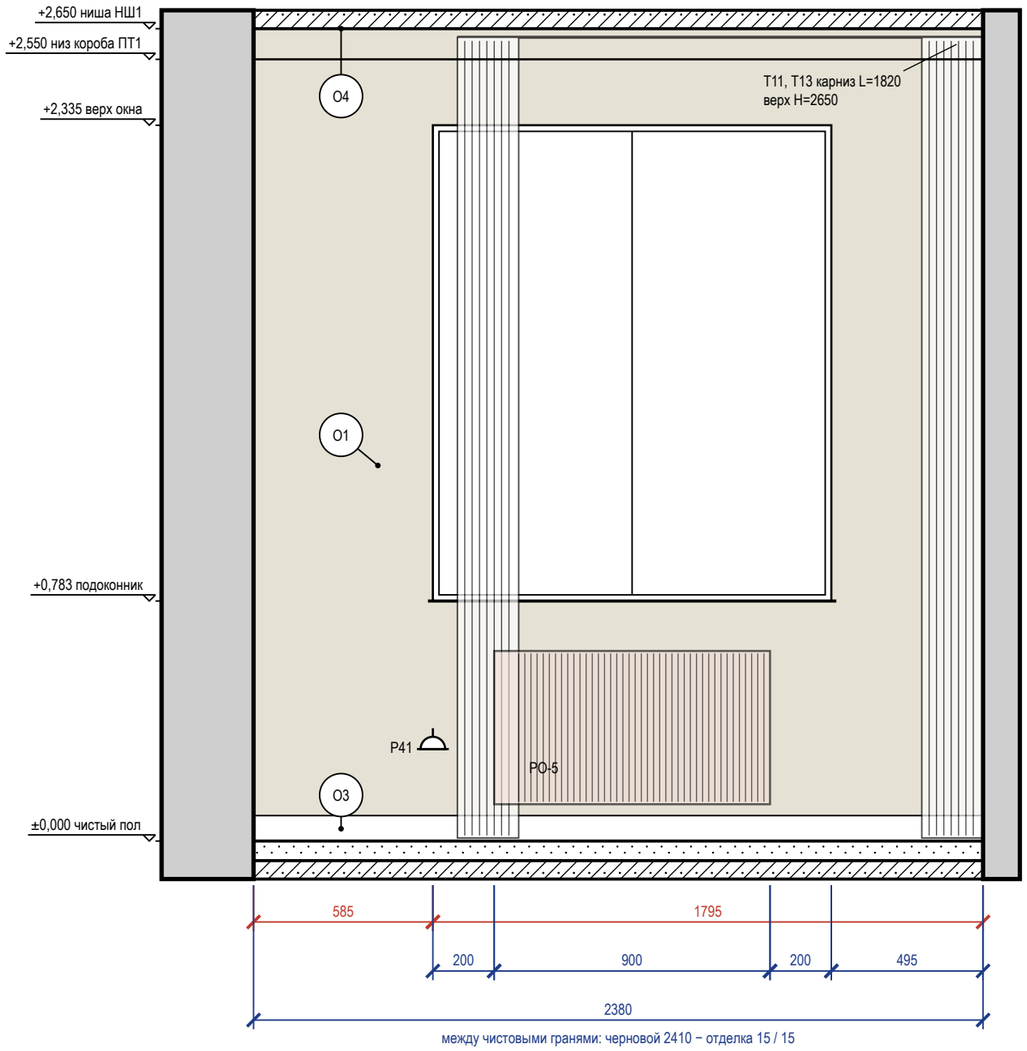

Ведомость точек и выводов

Марка	Что это	Гр.	H, мм	От угла, мм	Примечание
Р41	розетка: уборка	5	300	585	


Ведомость изделий и проёмов (на листе)

Марка	Изделие, проём	На виде Ш×В, мм	Низ, мм
РО-5	радиатор отопления	900×500	120

Примечания

1. Размеры — в мм от чистовых поверхностей стен; условные обозначения и общие указания — лист 22.
2. Карнизы (шины) — по ведомости текстиля декоратора: длина L и верх H на развёртке — те же числа, что в ведомости; крепление — до окраски потолка.
3. Карниз Т11, Т13: по ведомости текстиля шина L=1820 мм, а от её начала до чистового угла стены — 1715 мм: шина не встаёт, длину согласовать с декоратором до заказа.
4. Линии узора (швы плитки, складки штор, рёбра радиаторов) прерываются у знаков и выносок — просвет между линиями не менее 0,7 мм.


Стена Б — визуализация, лист 15

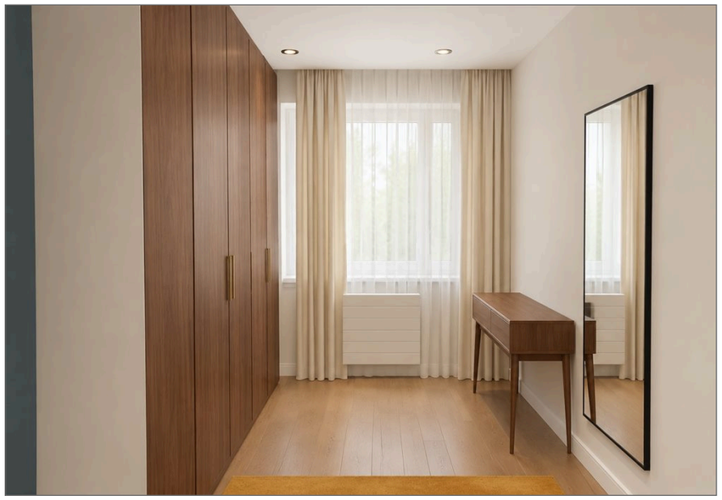

Ведомость отделки (на листе)

Марка	Поверхность	Материал, изделие	Цвет, код	Кол.
О1	стены	окраска, Farrow & Ball Modern Emulsion, матовая, подготовка Q3	Farrow & Ball No. 291 «School House White — тёплый меловой белый»	4,3 м²
О3	плинтус	плинтус МДФ, h 83 мм, Ultrawood Base 5340, ЛДФ под окраску, 83×15 мм, 2440 мм (арт. LDF-BASE-5340)	Farrow & Ball No. 291 «School House White — тёплый меловой белый»	2,4 м
О4	потолок	окраска, Tikkurila Anti-Reflex 2, глубокоматовая, подготовка Q3	NCS S 0502-Y «Белый с лёгкой желтизной»	11,4 м²


Схема развёрток (М 1:50)

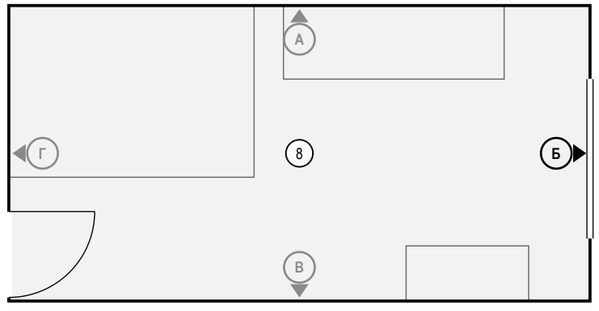

	Лист	№ док.	Подпись	Дата	Проект: Квартира 103 м²			М 1:20
Дизайнер	Кырлан А.С.			14.11.26	Развёртка стены Б. Спальня 2 (пом. 8)	Стадия	Лист	Листов
Проверил						П	91	129
Н. контр.								
Утв.								

выпуск 14.11.2026 № 32d0256903 · стр. 91 из 129

Стена В (М 1:20)

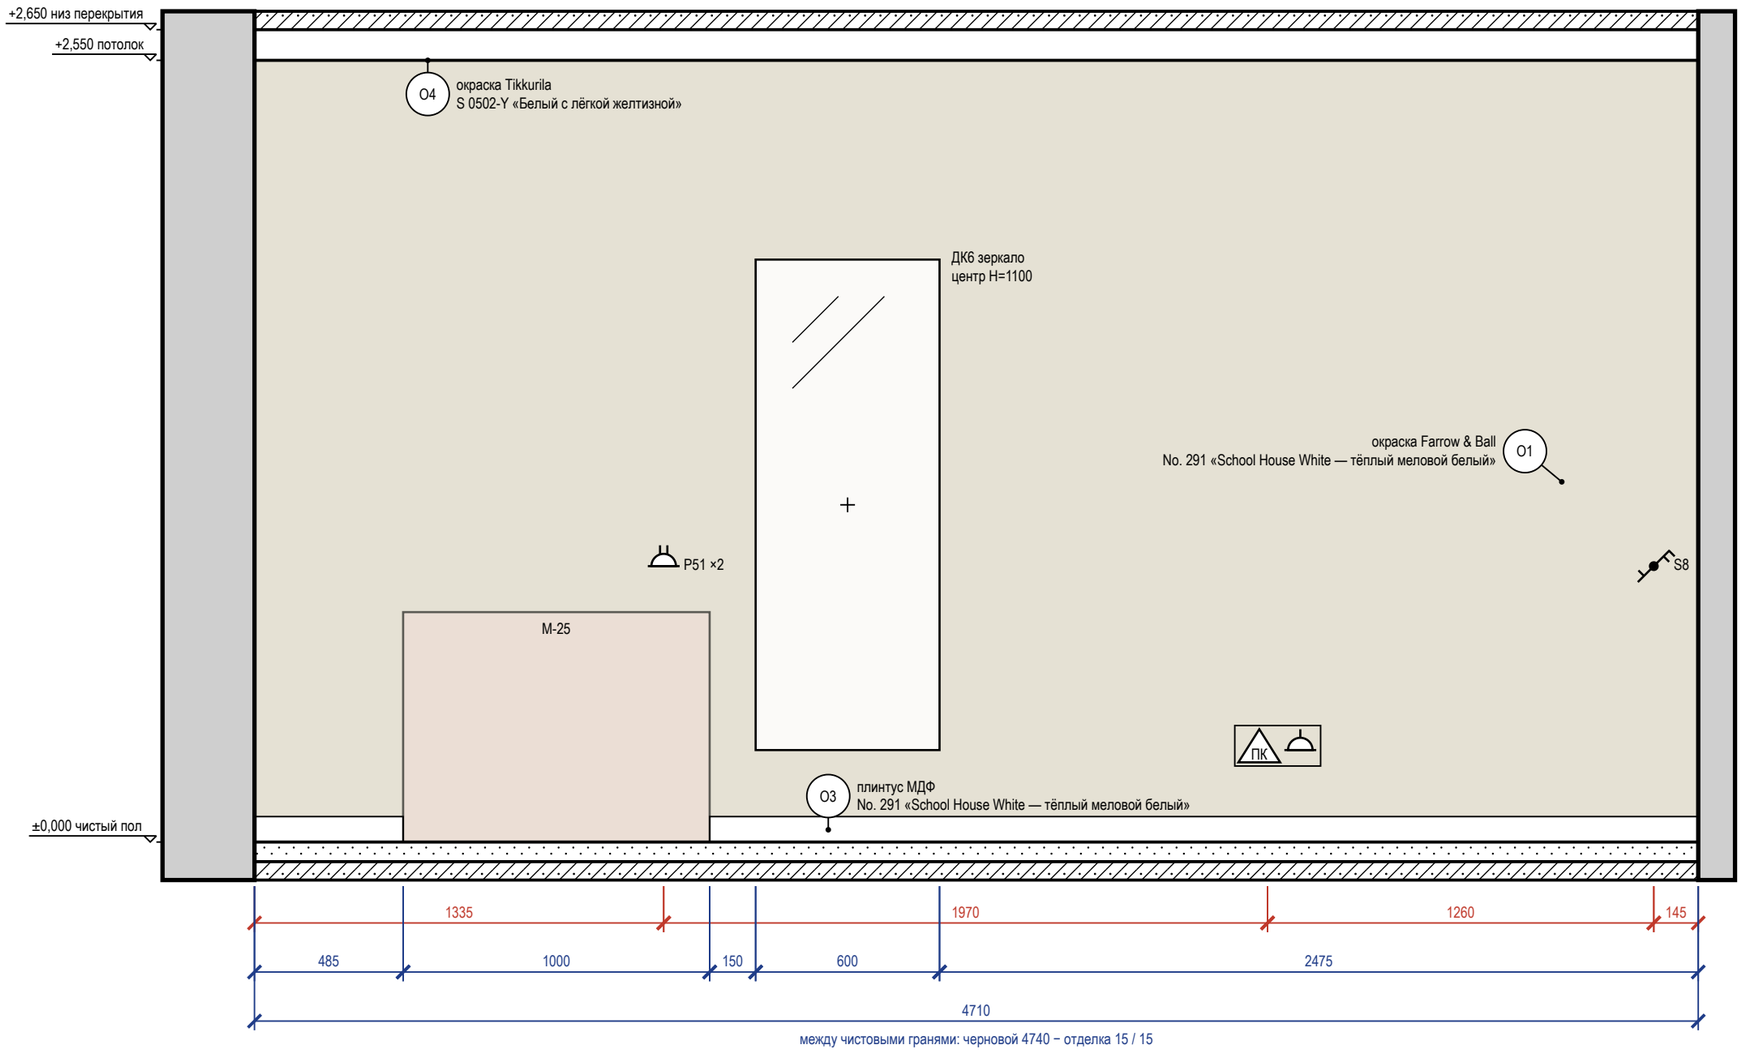


Ведомость точек и выводов

Марка	Что это	Гр.	H, мм	От угла, мм	Примечание
P51	розетка: туалетный столик: фен, подсветка зеркала	5	900	1335	рамка 2 поста
LAN3	розетка RJ45: передача данных		300	3305	
P39	розетка: общего назначения	5	300	3385	
S8	выключатель	1	900	4565	

Ведомость отделки (на листе)

Марка	Поверхность	Материал, изделие	Цвет, код	Кол.
О1	стены	окраска, Farrow & Ball Modern Emulsion, матовая, подготовка Q3	Farrow & Ball No. 291 «School House White тёплый меловой белый»	12 м²
О3	плинтус	плинтус МДФ, h 83 мм, Ultrawood Base 5340, ЛДФ под окраску, 83×15 мм, 2440 мм (арт. LDF-BASE-5340)	Farrow & Ball No. 291 «School House White тёплый меловой белый»	3,7 м
О4	потолок	окраска, Tikkurila Anti-Reflex 2, глубокоматовая, подготовка Q3	NCS S 0502-Y «Белый с лёгкой желтизной»	11,4 м²

Схема развёрток (М 1:100)

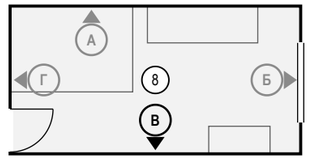


Примечания

1. Размеры — в мм от чистовых поверхностей стен; условные обозначения и общие указания — лист 22.
2. Картины и зеркала крепить к основанию по паспорту изделия (закладные и анкеры — в перечне скрытых работ); крест — ось центра предмета.
3. Часть марок не уместилась у знаков: коды, высоты и привязки этих позиций — в ведомости точек и выводов под видами.

	Лист	№ док.	Подпись	Дата	Проект: Квартира 103 м²			М 1:20
Дизайнер	Кырлан А.С.			14.11.26	Развёртка стены В. Спальня 2 (пом. 8)	Стадия	Лист	Листов
Проверил						П	92	129
Н. контр.								
Утв.								

Стена Г (М 1:20)

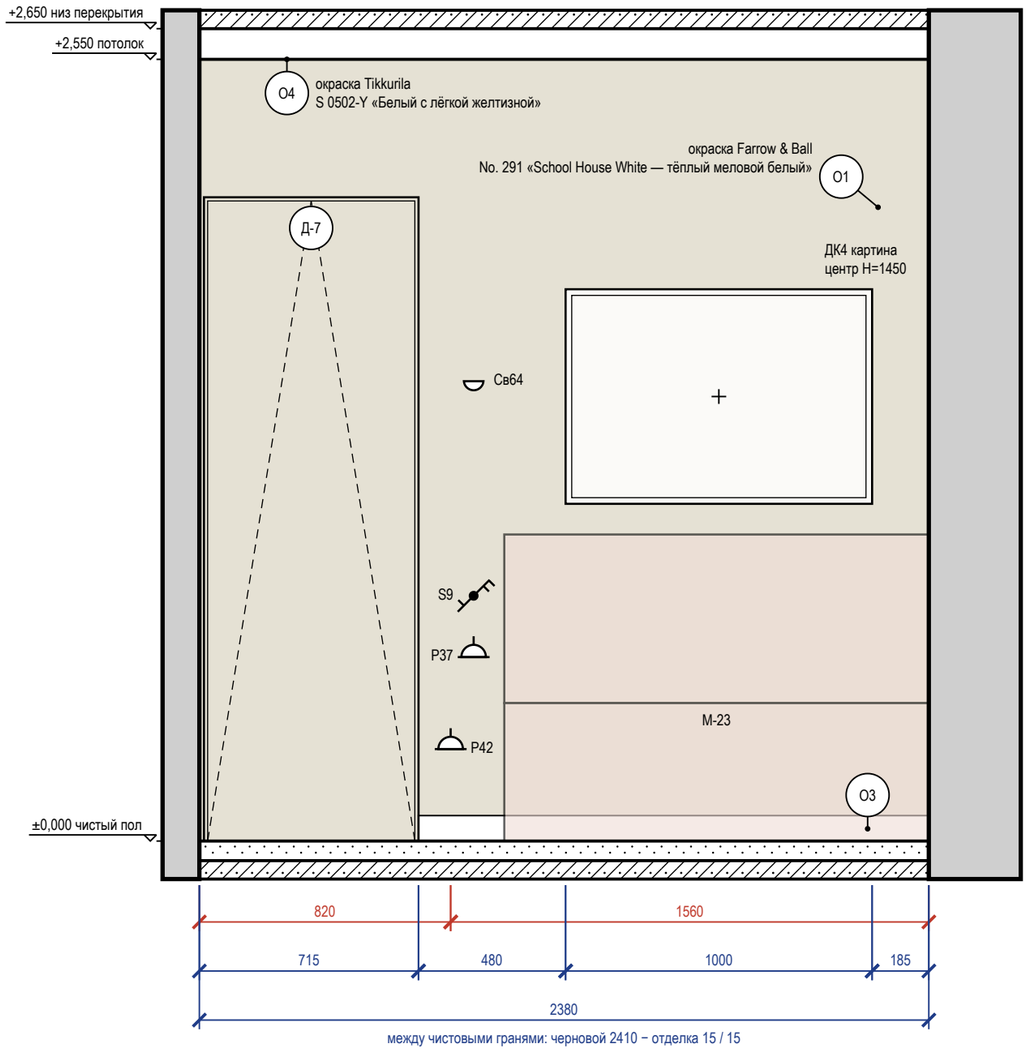

Ведомость отделки (на листе)

Марка	Поверхность	Материал, изделие	Цвет, код	Кол.
О1	стены	окраска, Farrow & Ball Modern Emulsion, матовая, подготовка Q3	Farrow & Ball No. 291 «School House White тёплый меловой белый»	4,6 м²
О3	плинтус	плинтус МДФ, h 83 мм, Ultrawood Base 5340, ЛДФ под окраску, 83×15 мм, 2440 мм (арт. LDF-BASE-5340)	Farrow & Ball No. 291 «School House White тёплый меловой белый»	1,7 м
О4	потолок	окраска, Tikkurila Anti-Reflex 2, глубокоматовая, подготовка Q3	NCS S 0502-Y «Белый с лёгкой желтизной»	11,4 м²

Примечания

1. Размеры — в мм от чистовых поверхностей стен; условные обозначения и общие указания — лист 22.
2. Картины и зеркала крепить к основанию по паспорту изделия (закладные и анкеры — в перечне скрытых работ); крест — ось центра предмета.
3. Двери скрытого монтажа — полотно в плоскости стены, отделка стены по полотну, плинтус прерывается у короба (узел — на листе узлов).

Ведомость точек и выводов

Марка	Что это	Гр.	Н, мм	От угла, мм	Примечание
Р42	розетка: уборка у входа	5	300	820	
Р37	розетка: у кровати	5	600	895	
S9	выключатель	1	800	895	
Св64	светильник настенный	1	1500	895	

Стена Г — визуализация, лист 16


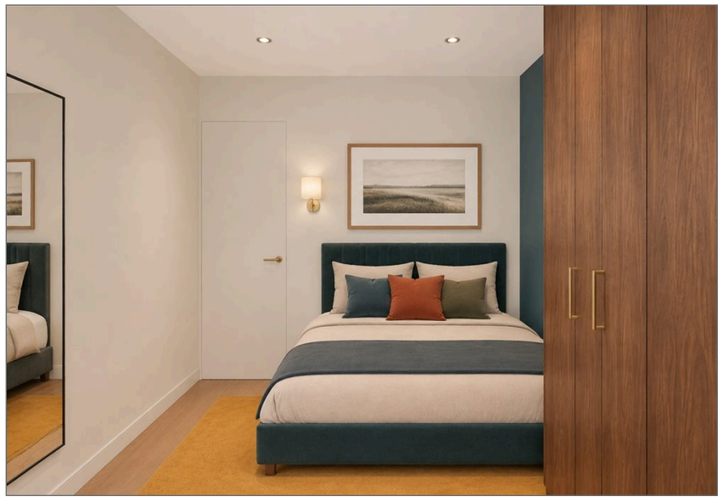


Схема развёрток (М 1:50)

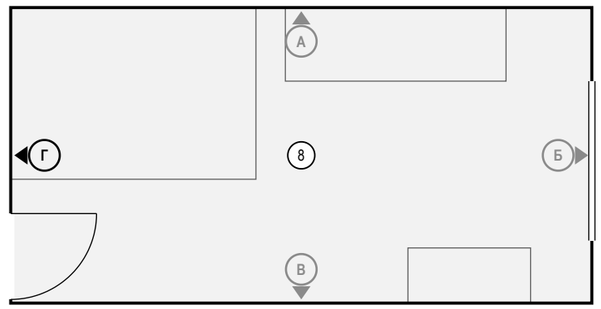


Ведомость изделий и проёмов (на листе)

Марка	Изделие, проём	На виде Ш×В, мм	Низ, мм
Д-7	дверь скрытого монтажа	700×2100	0
М-23	кровать 1400×2000, изголовье с каннелюрами, бархат цвета тил	1385×450	0
ДК4	картина	1000×700	1100

	Лист	№ док.	Подпись	Дата	Проект: Квартира 103 м²	М 1:20
Дизайнер	Кырлан А.С.			14.11.26	Развёртка стены Г. Спальня 2 (пом. 8)	Стадия: П; Лист: 93; Листов: 129
Проверил						
Н. контр.						
Утв.						

выпуск 14.11.2026 № 32d0256903 · стр. 93 из 129

Стена А (М 1:20)

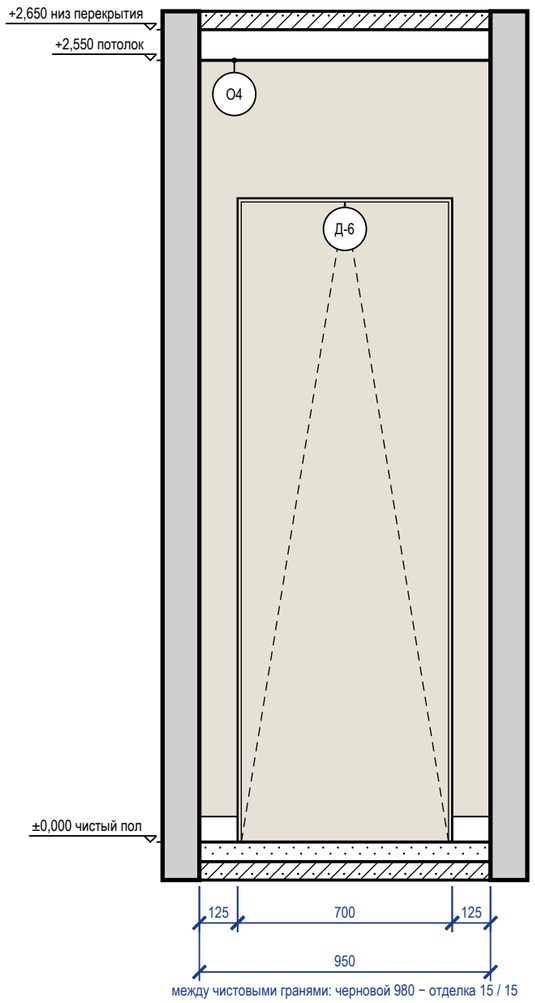

Стена В (М 1:20)


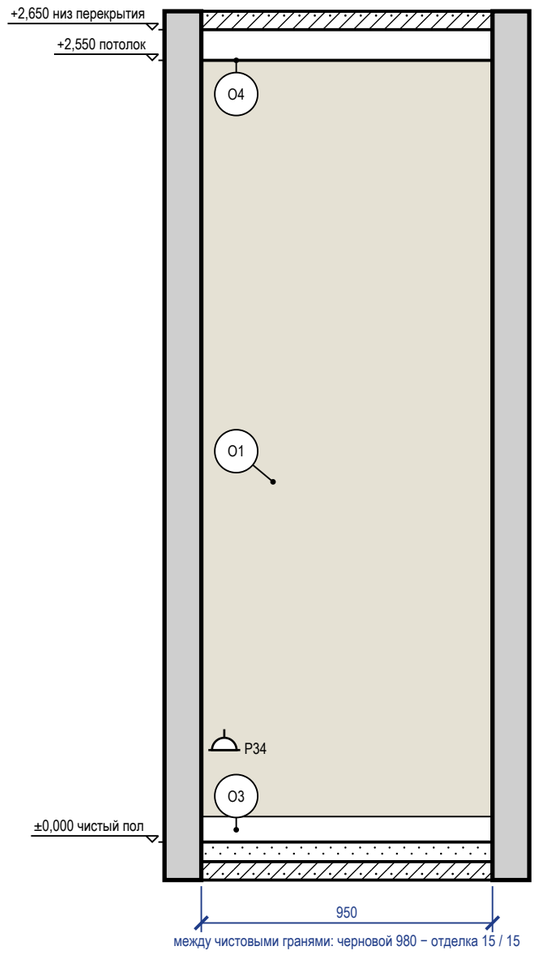


Схема развёрток (М 1:50)

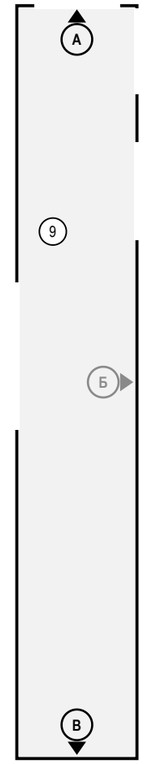

Ведомость точек и выводов

Стена	Марка	Что это	Гр.	Н, мм	От угла, мм	Примечание
В	Р34	розетка: уборка	6	300	75	

Ведомость отделки (на листе)

Марка	Поверхность	Материал, изделие	Цвет, код	Кол.
О1	стены	окраска, Farrow & Ball Modern Emulsion, матовая, подготовка Q3	Farrow & Ball No. 291 «School House White — тёплый меловой белый»	3,4 м²
О3	плинтус	плинтус МДФ, h 83 мм, Ultrawood Base 5340, ЛДФ под окраску, 83×15 мм, 2440 мм (арт. LDF-BASE-5340)	Farrow & Ball No. 291 «School House White — тёплый меловой белый»	1,2 м
О4	потолок	окраска, Tikkurila Anti-Reflex 2, глубокоматовая, подготовка Q3	NCS S 0502-Y «Белый с лёгкой желтизной»	6 м²

Ведомость изделий и проёмов (на листе)

Стена	Марка	Изделие, проём	На виде Ш×В, мм	Низ, мм
А	Д-6	дверь скрытого монтажа	700×2100	0

Примечания

1. Размеры — в мм от чистовых поверхностей стен; условные обозначения и общие указания — лист 22.
2. Двери скрытого монтажа — полотно в плоскости стены, отделка стены по полотну, плинтус прерывается у короба (узел — на листе узлов).

	Лист	№ док.	Подпись	Дата
Дизайнер	Кырлан А.С.			14.11.26
Проверил				
Н. контр.				
Утв.				


Проект: Квартира 103 м² — М 1:20

Развёртки стен А, В. Коридор (пом. 9)

Стадия	Лист	Листов
П	94	129

выпуск 14.11.2026 № 32d0256903 · стр. 94 из 129


Стена Б (М 1:20)

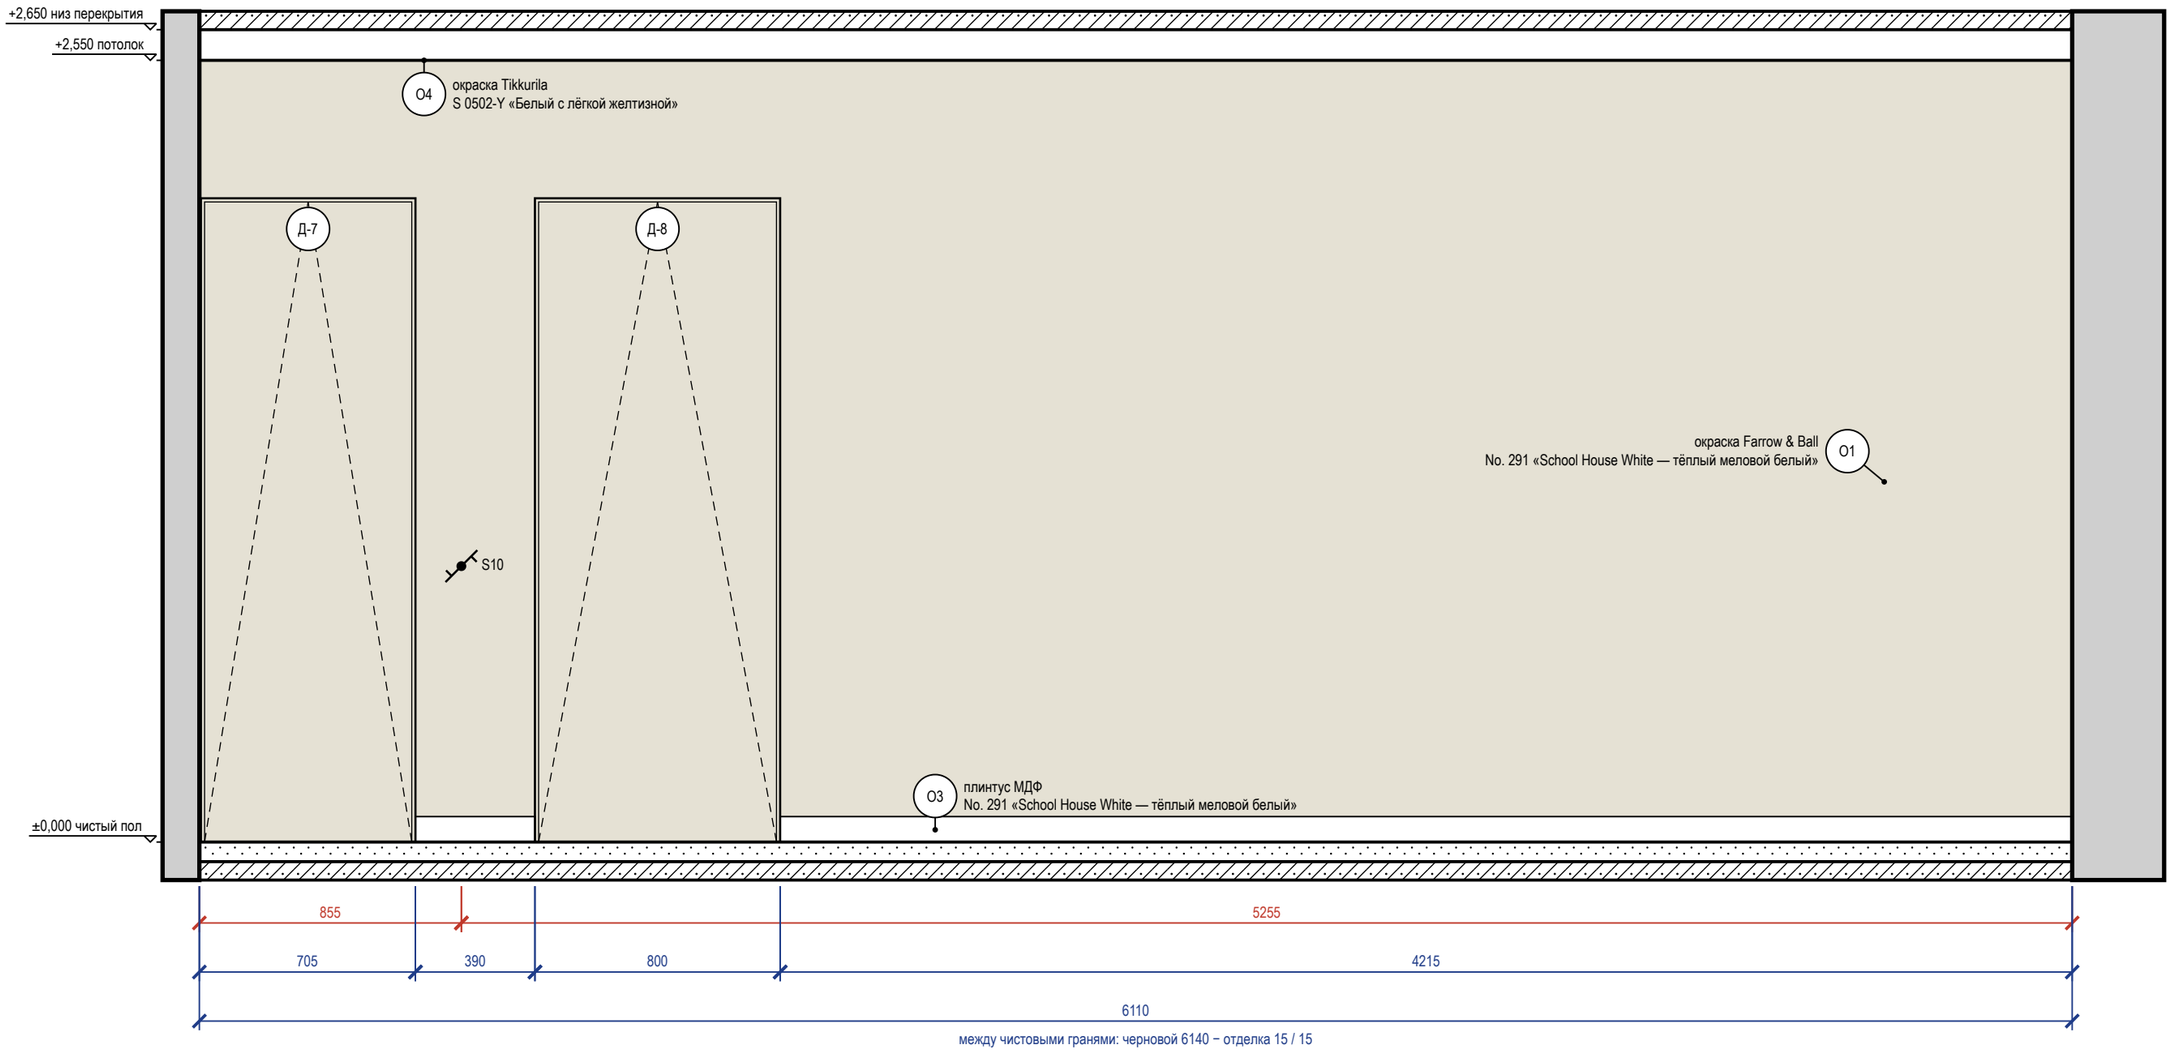

Ведомость точек и выводов

Марка	Что это	Гр.	Н, мм	От угла, мм	Примечание
S10	выключатель	2	900	855	

Стена Б — визуализация, лист 17

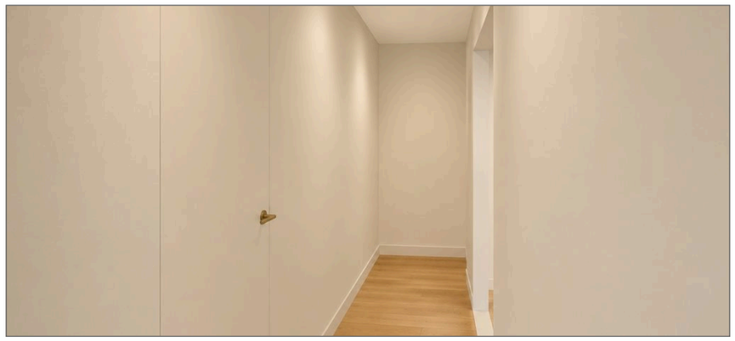

Ведомость изделий и проёмов (на листе)

Марка	Изделие, проём	На виде Ш×В, мм	Низ, мм
Д-7	дверь скрытого монтажа	700×2100	0
Д-8	дверь скрытого монтажа	800×2100	0

Примечания

1. Размеры — в мм от чистовых поверхностей стен; условные обозначения и общие указания — лист 22.
2. Отделка стен — по ведомости отделки помещений, лист С1.
3. Двери скрытого монтажа — полотно в плоскости стены, отделка стены по полотну, плинтус прерывается у короба (узел — на листе узлов).

	Лист	№ док.	Подпись	Дата
Дизайнер	Кырлан А.С.			14.11.26
Проверил				
Н. контр.				
Утв.				

Проект: Квартира 103 м² — **М 1:20**

Развёртка стены Б. Коридор (пом. 9)

Стадия	Лист	Листов
П	95	129

выпуск 14.11.2026 № 32d0256903 · стр. 95 из 129

Стена А (М 1:20)


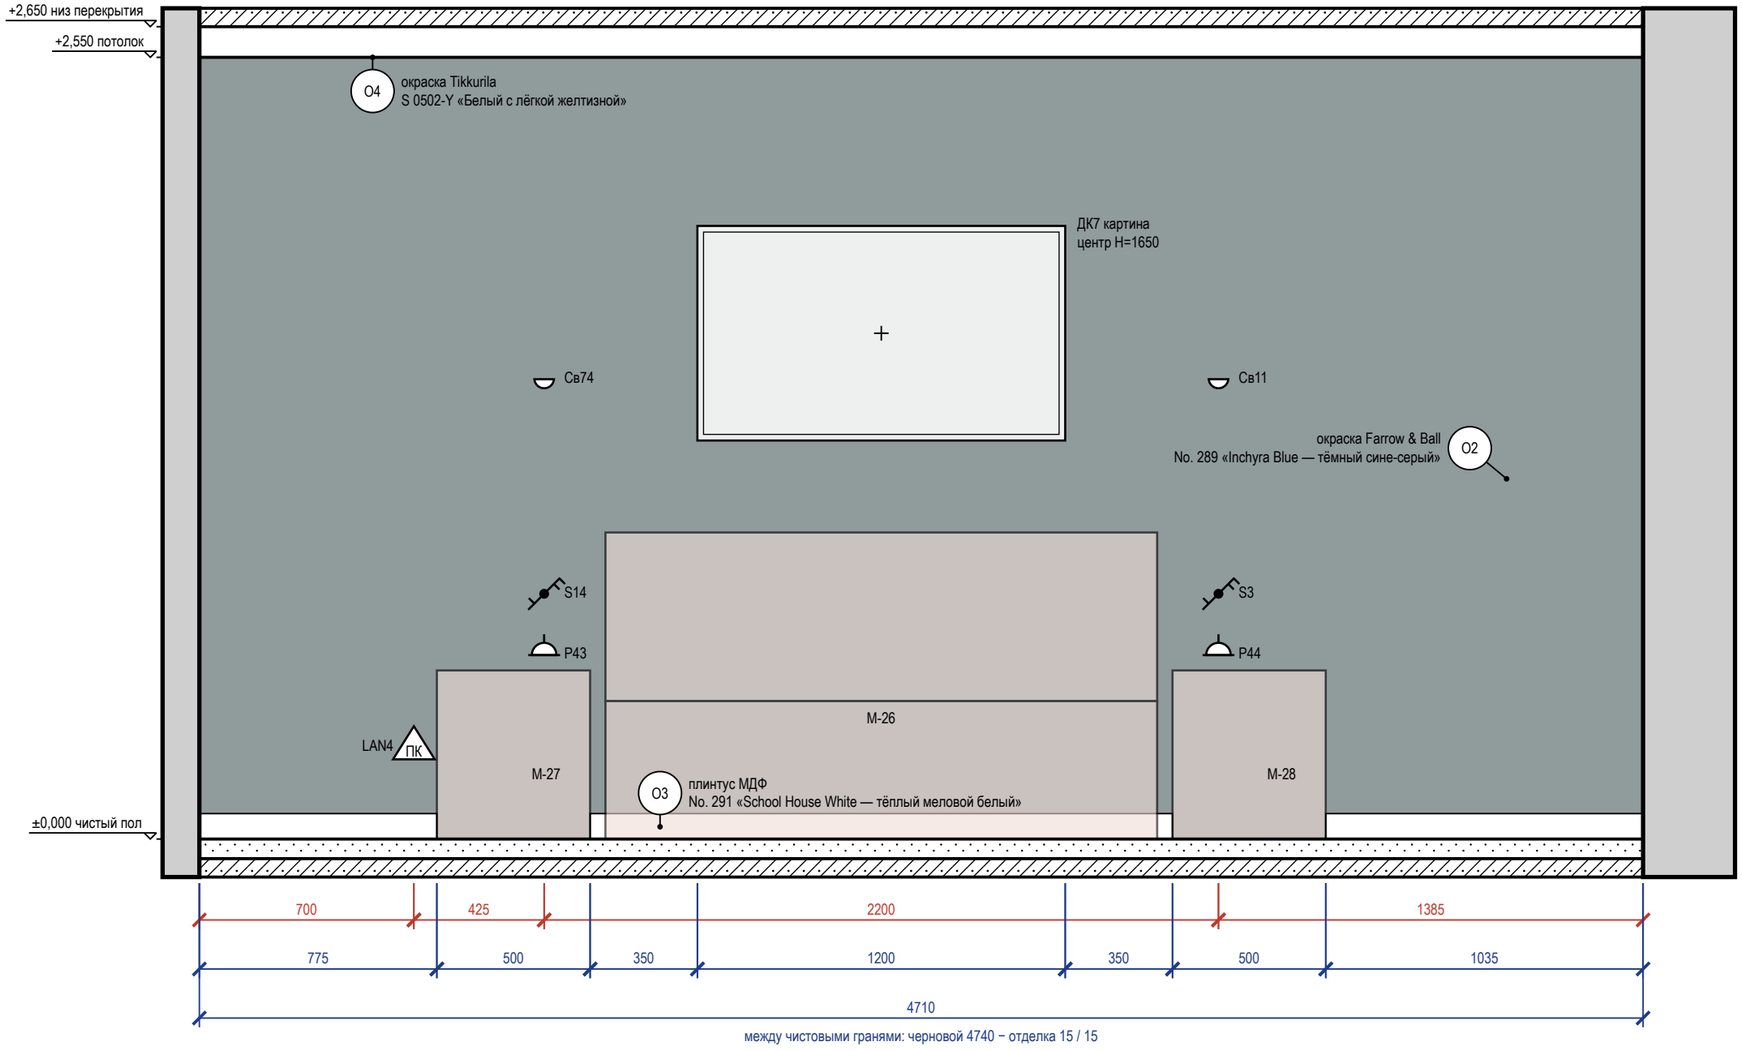


Схема развёрток (М 1:100)

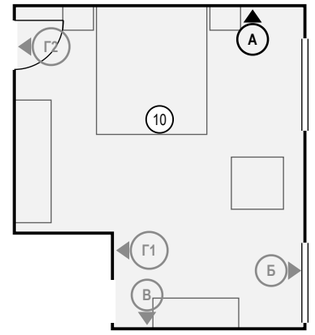

Ведомость точек и выводов

Марка	Что это	Гр.	Н, мм	От угла, мм	Примечание
LAN4	розетка RJ45: передача данных		300	700	
P43	розетка: у кровати	4	600	1125	
S14	выключатель	1	800	1125	
Св74	светильник настенный	1	1500	1125	
P44	розетка: у кровати	4	600	3325	
S3	выключатель	1	800	3325	
Св11	светильник настенный	1	1500	3325	

Стена А — визуализация, лист 18



Ведомость изделий и проёмов (на листе)

Марка	Изделие, проём	На виде Ш×В, мм	Низ, мм
М-27	тумба прикроватная, орех и латунь	500×550	0
М-26	кровать 1800×2100 с высоким изголовьем ар-деко, изумрудный бархат, латунный кант	1800×450	0
ДК7	картина	1200×700	1300
М-28	тумба прикроватная, орех и латунь	500×550	0

Примечания

1. Размеры — в мм от чистовых поверхностей стен; условные обозначения и общие указания — лист 22.
2. Отделка стен — по ведомости отделки помещений, лист С1.
3. Картины и зеркала крепить к основанию по паспорту изделия (закладные и анкеры — в перечне скрытых работ); крест — ось центра предмета.

	Лист	№ док.	Подпись	Дата
Дизайнер	Кырлан А.С.			14.11.26
Проверил				
Н. контр.				
Утв.				


Проект: Квартира 103 м² — **М 1:20**

Развёртка стены А. Спальня мастер (пом. 10)

Стадия	Лист	Листов
П	96	129

выпуск 14.11.2026 № 32d0256903 · стр. 96 из 129


Стена Б (М 1:20)

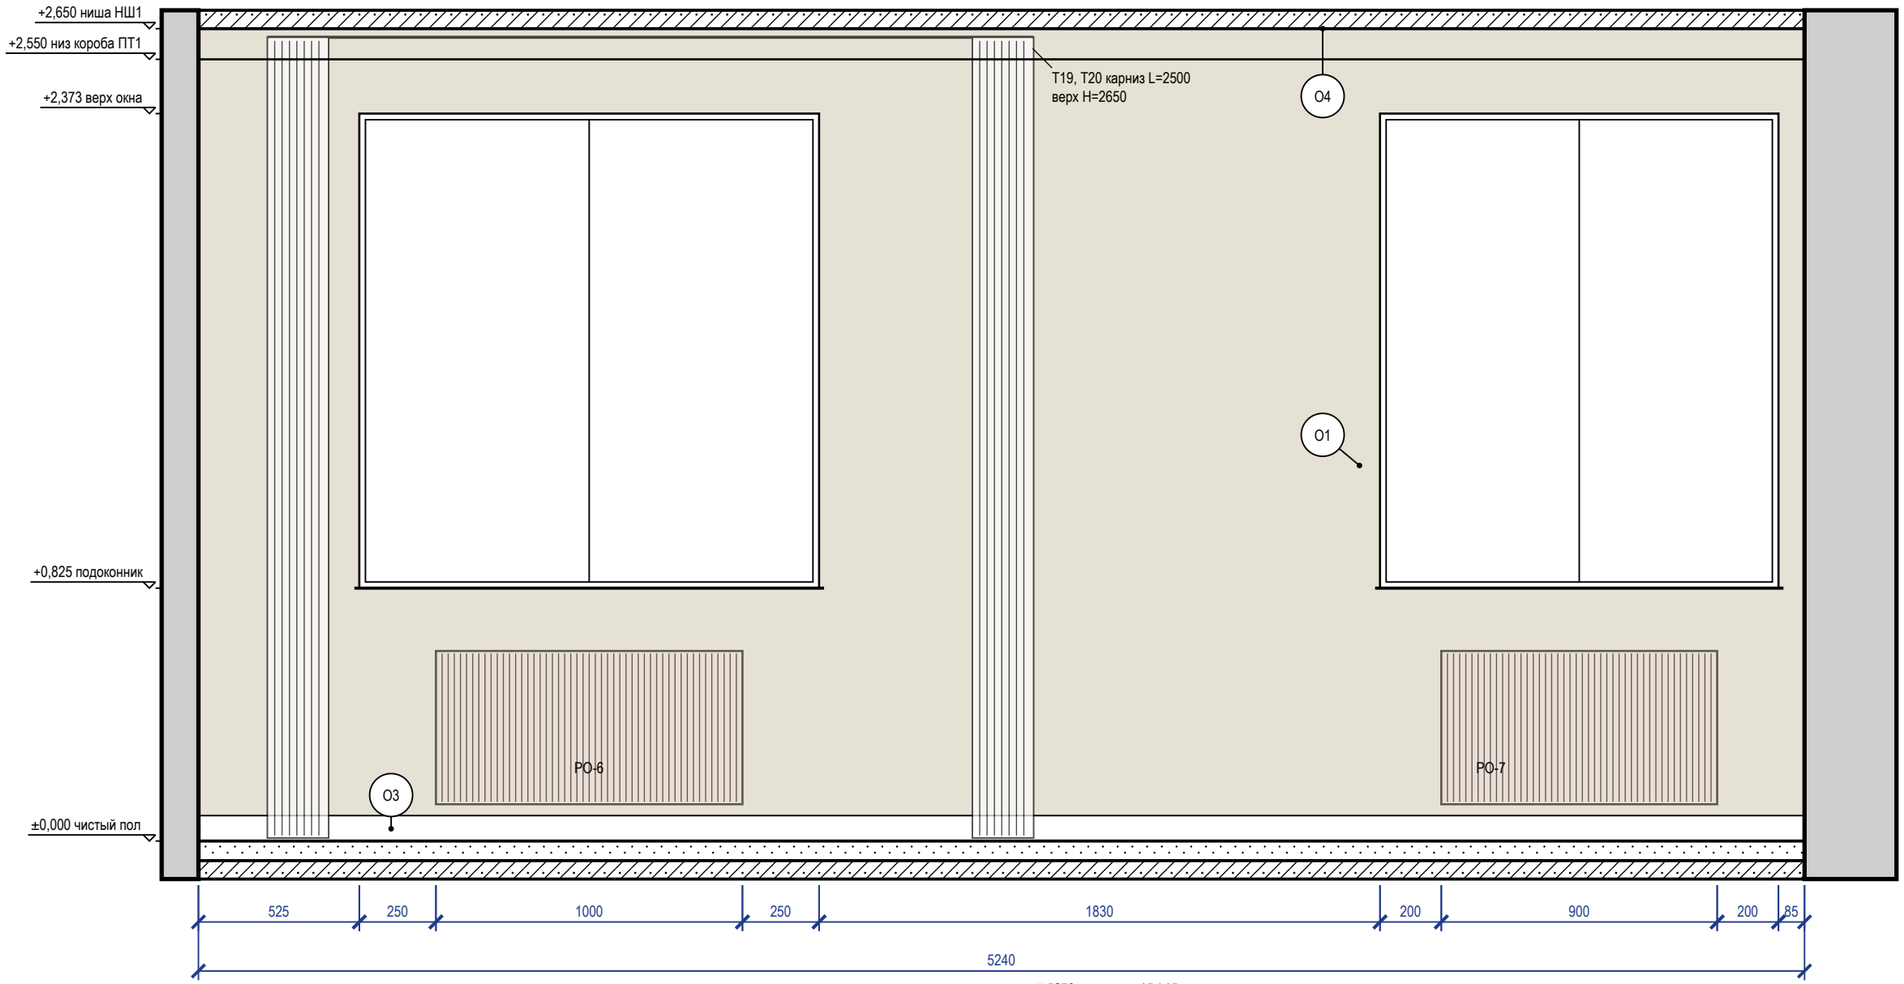

Ведомость отделки (на листе)

Марка	Поверхность	Материал, изделие	Цвет, код	Кол.
О1	стены	окраска, Farrow & Ball Modern Emulsion, матовая, подготовка Q3	Farrow & Ball No. 291 «School House White — тёплый меловой белый»	9,6 м²
О3	плинтус	плинтус МДФ, h 83 мм, Ultrawood Base 5340, ЛДФ под окраску, 83×15 мм, 2440 мм (арт. LDF-BASE-5340)	Farrow & Ball No. 291 «School House White — тёплый меловой белый»	5,2 м
О4	потолок	окраска, Tikkurila Anti-Reflex 2, глубокоматовая, подготовка Q3	NCS S 0502-Y «Белый с лёгкой желтизной»	22,5 м²

Схема развёрток (М 1:100)

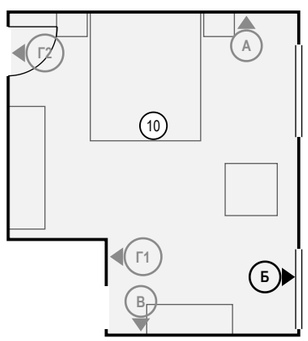

Ведомость изделий и проёмов (на листе)

Марка	Изделие, проём	На виде Ш×В, мм	Низ, мм
РО-6	радиатор отопления	1000×500	120
РО-7	радиатор отопления	900×500	120

Примечания

1. Размеры — в мм от чистовых поверхностей стен; условные обозначения и общие указания — лист 22.
2. Карнизы (шины) — по ведомости текстиля декоратора: длина L и верх H на развёртке — те же числа, что в ведомости; крепление — до окраски потолка.

	Лист	№ док.	Подпись	Дата
Дизайнер	Кырлан А.С.			14.11.26
Проверил				
Н. контр.				
Утв.				


Проект: Квартира 103 м² — **М 1:20**

Развёртка стены Б. Спальня мастер (пом. 10)


Стадия	Лист	Листов
П	97	129

выпуск 14.11.2026 № 32d0256903 · стр. 97 из 129

Стена В (М 1:20)

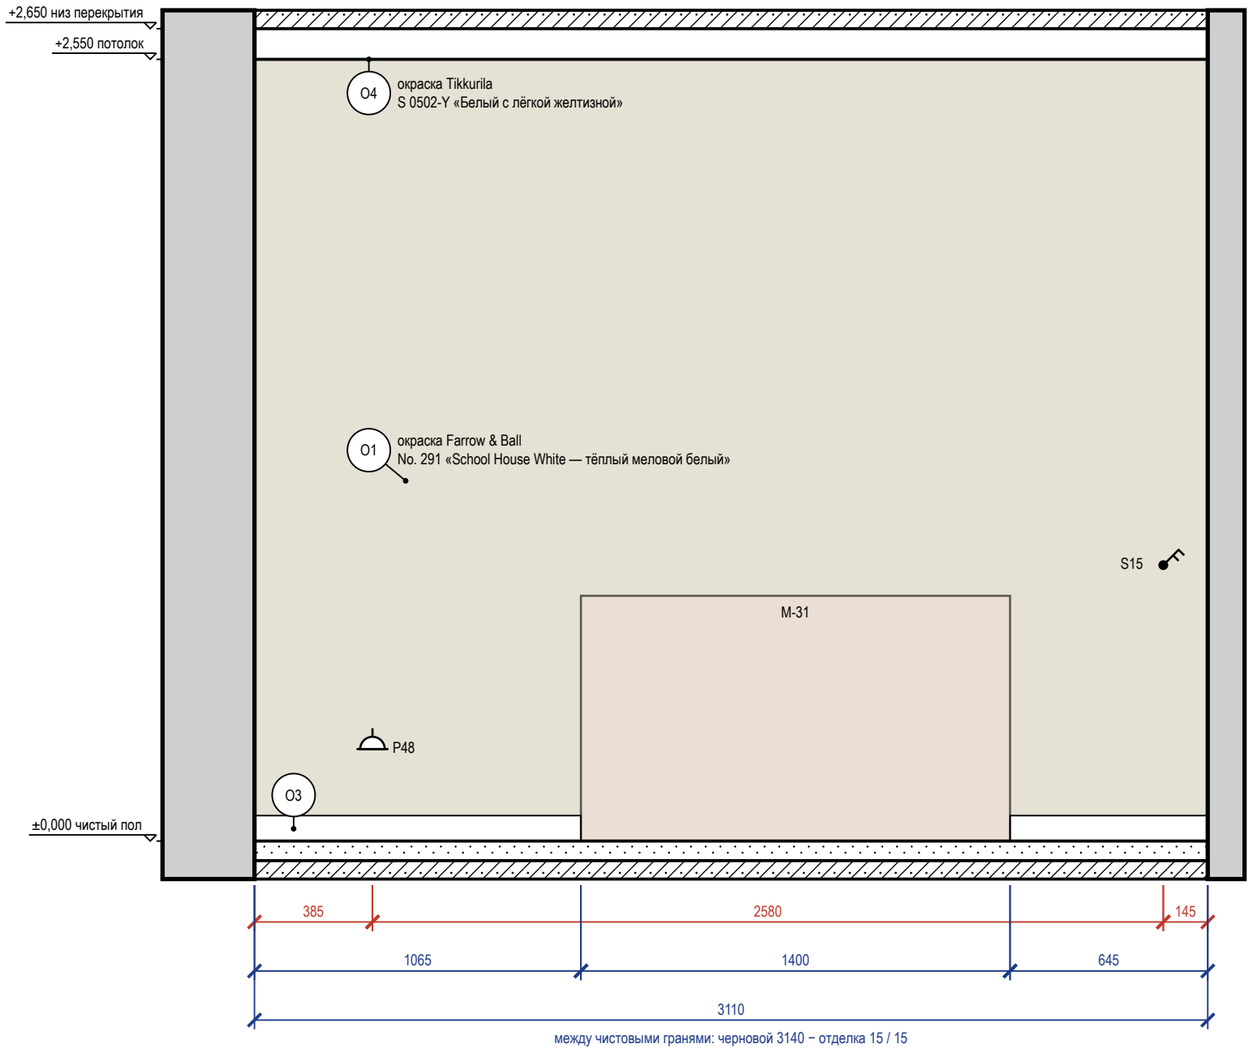

Стена В — визуализация, лист 19

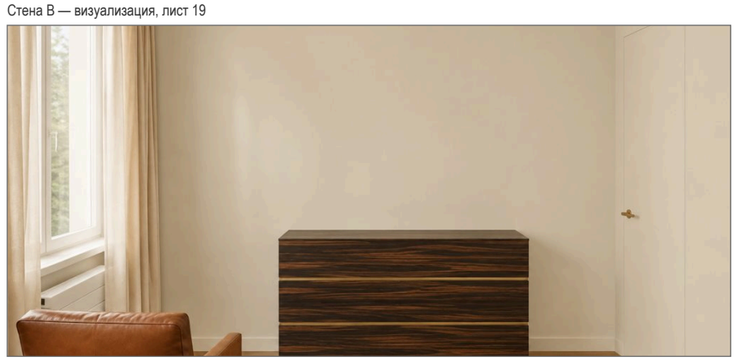

Примечания

1. Размеры — в мм от чистовых поверхностей стен; условные обозначения и общие указания — лист 22.


Ведомость точек и выводов

Марка	Что это	Гр.	Н, мм	От угла, мм	Примечание
Р48	розетка: уборка	4	300	385	
S15	выключатель	3	900	2965	

Ведомость отделки (на листе)

Марка	Поверхность	Материал, изделие	Цвет, код	Кол.
О1	стены	окраска, Farrow & Ball Modern Emulsion, матовая, подготовка Q3	Farrow & Ball No. 291 «School House White — тёплый меловой белый»	7,9 м²
О3	плинтус	плинтус МДФ, h 83 мм, Ultrawood Base 5340, ЛДФ под окраску, 83×15 мм, 2440 мм (арт. LDF-BASE-5340)	Farrow & Ball No. 291 «School House White — тёплый меловой белый»	1,7 м
О4	потолок	окраска, Tikkurila Anti-Reflex 2, глубокоматовая, подготовка Q3	NCS S 0502-Y «Белый с лёгкой желтизной»	22,5 м²

Схема развёрток (М 1:50)

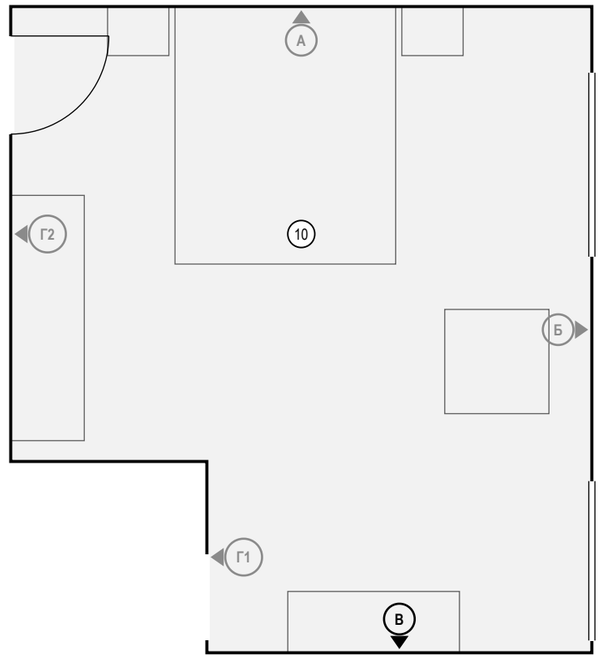

Ведомость изделий и проёмов (на листе)

Марка	Изделие, проём	На виде Ш×В, мм	Низ, мм
М-31	комод ар-деко, макассар и латунь	1400×800	0

	Лист	№ док.	Подпись	Дата
Дизайнер	Кырлан А.С.			14.11.26
Проверил				
Н. контр.				
Утв.				

Проект: Квартира 103 м² — **М 1:20**

Развёртка стены В. Спальня мастер (пом. 10)

Стадия	Лист	Листов
П	98	129

Стена Г1 (М 1:20)


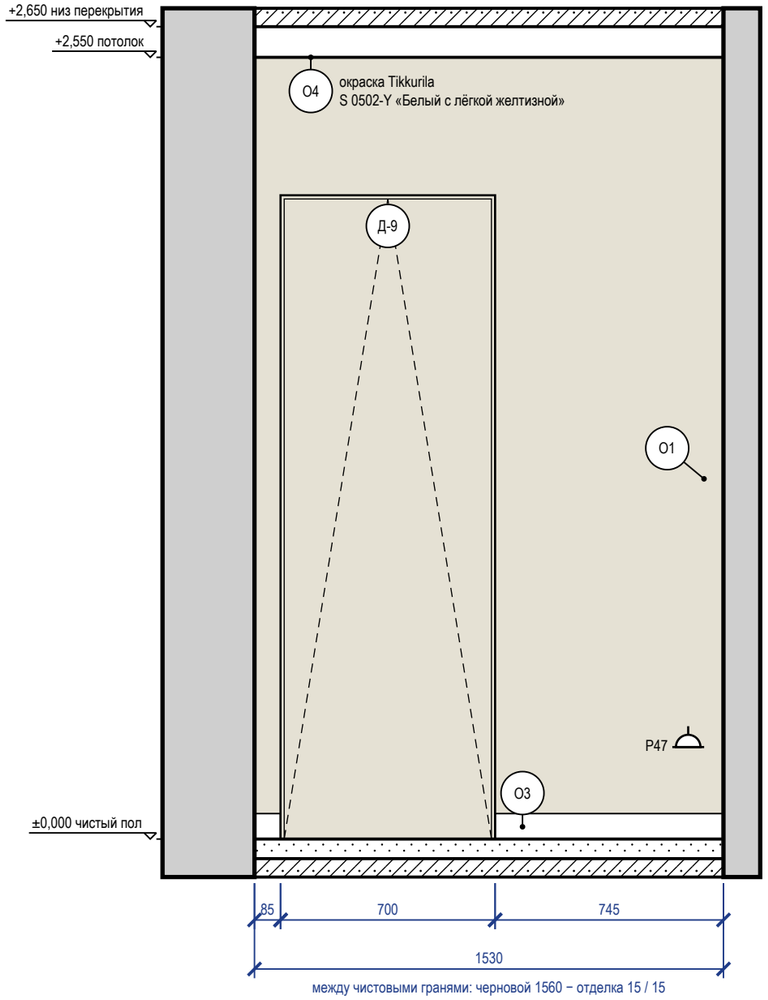


Схема развёрток (М 1:50)

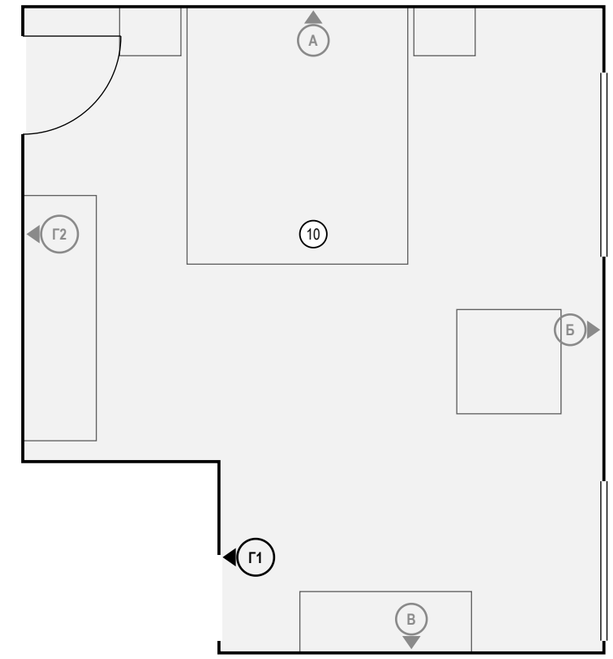

Ведомость точек и выводов

Марка	Что это	Гр.	Н, мм	От угла, мм	Примечание
Р47	розетка: общего назначения	4	300	1415	

Ведомость отделки (на листе)

Марка	Поверхность	Материал, изделие	Цвет, код	Кол.
О1	стены	окраска, Farrow & Ball Modern Emulsion, матовая, подготовка Q3	Farrow & Ball No. 291 «School House White — тёплый меловой белый»	2,4 м²
О3	плинтус	плинтус МДФ, h 83 мм, Ultrawood Base 5340, ЛДФ под окраску, 83×15 мм, 2440 мм (арт. LDF-BASE-5340)	Farrow & Ball No. 291 «School House White — тёплый меловой белый»	0,8 м
О4	потолок	окраска, Tikkurila Anti-Reflex 2, глубокоматовая, подготовка Q3	NCS S 0502-Y «Белый с лёгкой желтизной»	22,5 м²

Ведомость изделий и проёмов (на листе)

Марка	Изделие, проём	На виде Ш×В, мм	Низ, мм
Д-9	дверь скрытого монтажа	700×2100	0

Примечания

1. Размеры — в мм от чистовых поверхностей стен; условные обозначения и общие указания — лист 22.
2. Двери скрытого монтажа — полотно в плоскости стены, отделка стены по полотну, плинтус прерывается у короба (узел — на листе узлов).

	Лист	№ док.	Подпись	Дата
Дизайнер	Кырлан А.С.			14.11.26
Проверил				
Н. контр.				
Утв.				


Проект: Квартира 103 м² — **М 1:20**

Развёртка стены Г1. Спальня мастер (пом. 10)


Стадия	Лист	Листов
П	99	129

выпуск 14.11.2026 № 32d0256903 · стр. 99 из 129

Стена Г2 (М 1:20)

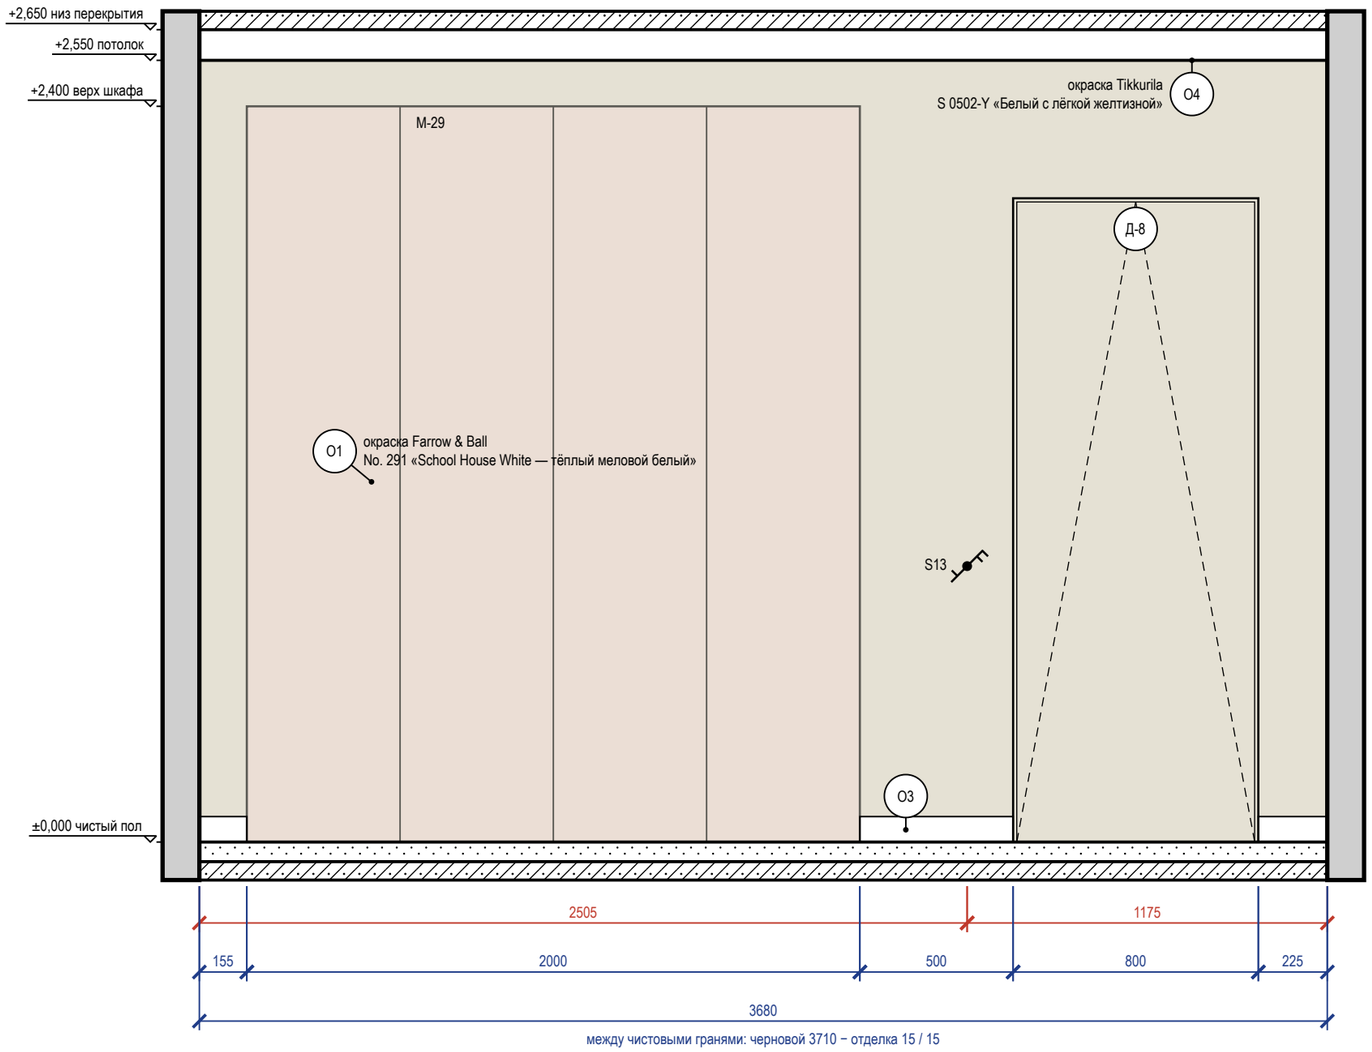

Стена Г2 — визуализация, лист 20

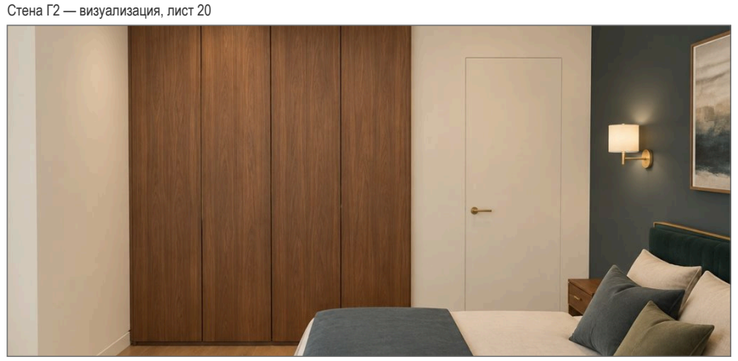

Ведомость изделий и проёмов (на листе)

Марка	Изделие, проём	На виде Ш×В, мм	Низ, мм
М-29	шкаф распашной	2000×2400	0
Д-8	дверь скрытого монтажа	800×2100	0

Примечания

1. Размеры — в мм от чистовых поверхностей стен; условные обозначения и общие указания — лист 22.
2. Двери скрытого монтажа — полотно в плоскости стены, отделка стены по полотну, плинтус прерывается у короба (узел — на листе узлов).


Ведомость точек и выводов

Марка	Что это	Гр.	Н, мм	От угла, мм	Примечание
S13	выключатель	1	900	2505	

Ведомость отделки (на листе)

Марка	Поверхность	Материал, изделие	Цвет, код	Кол.
О1	стены	окраска, Farrow & Ball Modern Emulsion, матовая, подготовка Q3	Farrow & Ball No. 291 «School House White — тёплый меловой белый»	7,7 м²
О3	плинтус	плинтус МДФ, h 83 мм, Ultrawood Base 5340, ЛДФ под окраску, 83×15 мм, 2440 мм (арт. LDF-BASE-5340)	Farrow & Ball No. 291 «School House White — тёплый меловой белый»	0,9 м
О4	потолок	окраска, Tikkurila Anti-Reflex 2, глубокоматовая, подготовка Q3	NCS S 0502-Y «Белый с лёгкой желтизной»	22,5 м²

Схема развёрток (М 1:50)

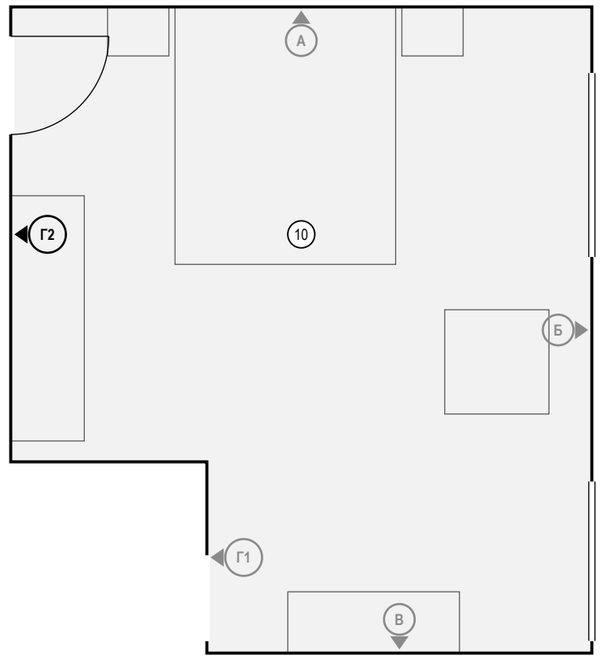


	Лист	№ док.	Подпись	Дата
Дизайнер	Кырлан А.С.			14.11.26
Проверил				
Н. контр.				
Утв.				

Проект: Квартира 103 м² — **М 1:20**

Развёртка стены Г2. Спальня мастер (пом. 10)


Стадия	Лист	Листов
П	100	129

Стена А (М 1:20)

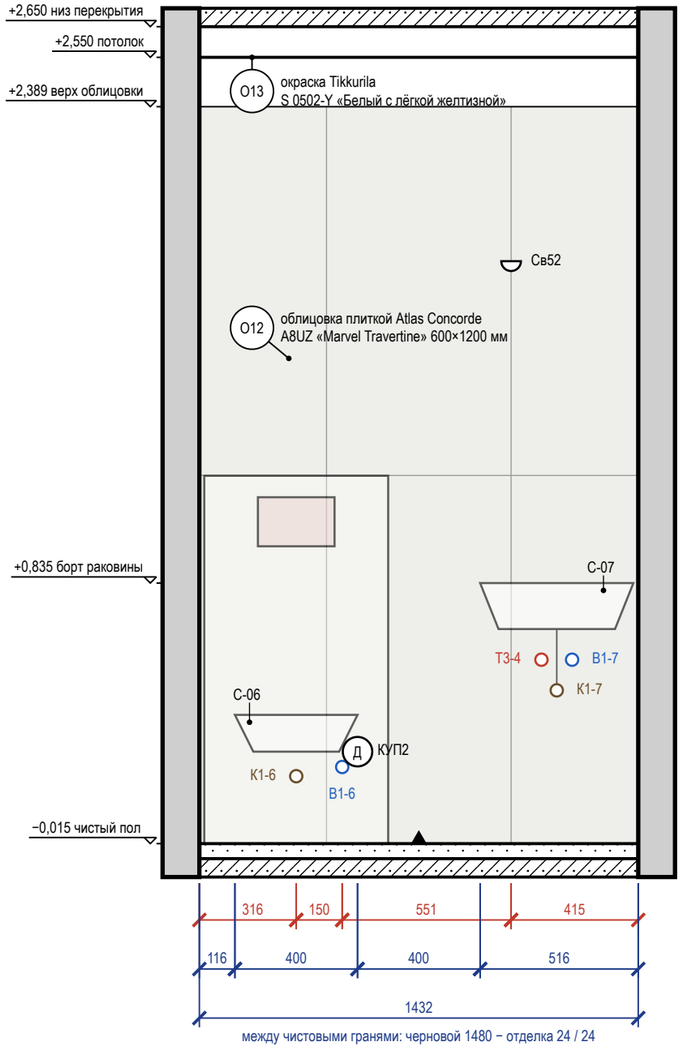

между чистовыми гранями: черновой 1480 − отделка 24 / 24

Стена Б (М 1:20)

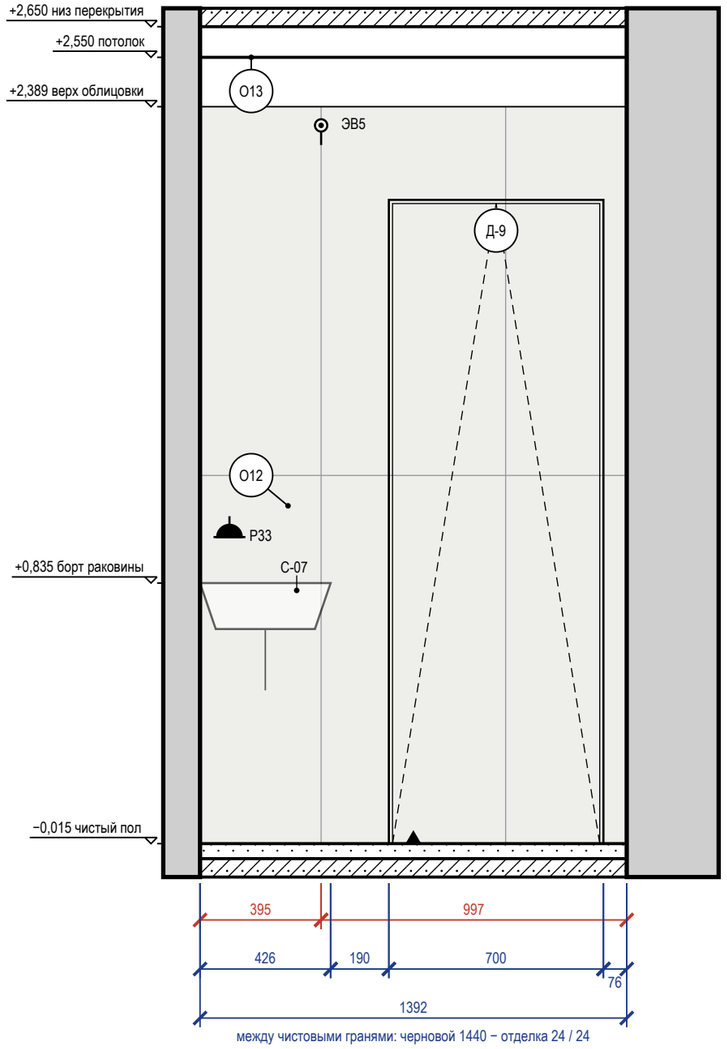

между чистовыми гранями: черновой 1440 − отделка 24 / 24

Ведомость точек и выводов

Стена	Марка	Что это	Гр.	Н, мм	От угла, мм	Примечание
А	К1-6	канализация — унитаз подвесной		220	316	Ø110
А	В1-6	холодная вода — унитаз подвесной		250	466	в раме инсталляции
А	КУП2	КУП (уравнивание потенциалов): КУП уравнивание потенциалов (ДСУП)		300	516	
А	Св52	светильник настенный	3	1900	1017	
А	Т3-4	горячая вода — умывальник		600	1116	межос. 100
А	К1-7	канализация — умывальник		500	1166	Ø50
А	В1-7	холодная вода — умывальник		600	1216	межос. 100
Б	Р33	розетка: фен у умывальника	7	1000	96	IP44
Б	ЭВ5	вывод кабеля: вентилятор ВР3 (таймер выбега)	3	2343	395	


Стена А — визуализация, лист 21



Ведомость отделки (на листе)

Марка	Поверхность	Материал, изделие	Цвет, код	Кол.
О12	стены	облицовка плиткой, Atlas Concorde Marvel Travertine, 600×1200×9 мм, A8UZ, затирка CG2WA	Atlas Concorde A8UZ «Marvel Travertine»	5,3 м²
О13	потолок	окраска, Tikkurila Luja 7, матовая, подготовка Q3	NCS S 0502-Y «Белый с лёгкой желтизной»	2,1 м²

Схема развёрток (М 1:50)

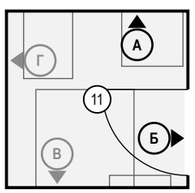

Ведомость изделий и проёмов (на листе)

Стена	Марка	Изделие, проём	На виде Ш×В, мм	Низ, мм
А	С-06	унитаз подвесной	400×120	300
А	С-07	раковина на консоли, латунный смеситель	500×150	700
Б	С-07	раковина на консоли, латунный смеситель	426×150	700
Б	Д-9	дверь скрытого монтажа	700×2100	0

Примечания


1. Размеры — в мм от чистовых поверхностей стен; условные обозначения и общие указания — лист 22.
2. Схема мебели, приборов и декора не является технической документацией для производства мебели; габариты — по паспортам изделий.
3. Выводы ВК — коды и высоты по листу выводов сантехники.
4. Облицовка — по сетке швов 2 мм, раскладка от оси стены (треугольник у пола), целые ряды от пола; подрезки — по листу раскладки плитки.
5. Гидроизоляция в 2 слоя, заход на стены 200 мм; у душа — до 2000 и 500 мм за поддон — до облицовки, с актом скрытых работ и тестом проливом (узел — на листе узлов).
6. Двери скрытого монтажа — полотно в плоскости стены, отделка стены по полотну, плинтус прерывается у короба (узел — на листе узлов).

	Лист	№ док.	Подпись	Дата	Проект: Квартира 103 м²	М 1:20
Дизайнер	Кырлан А.С.			14.11.26	Развёртки стен А, Б. Ванная мастер (пом. 11)	
Проверил						
Н. контр.						
Утв.						


Стадия	Лист	Листов
П	101	129

выпуск 14.11.2026 № 32d0256903 · стр. 101 из 129

Стена В (М 1:20)

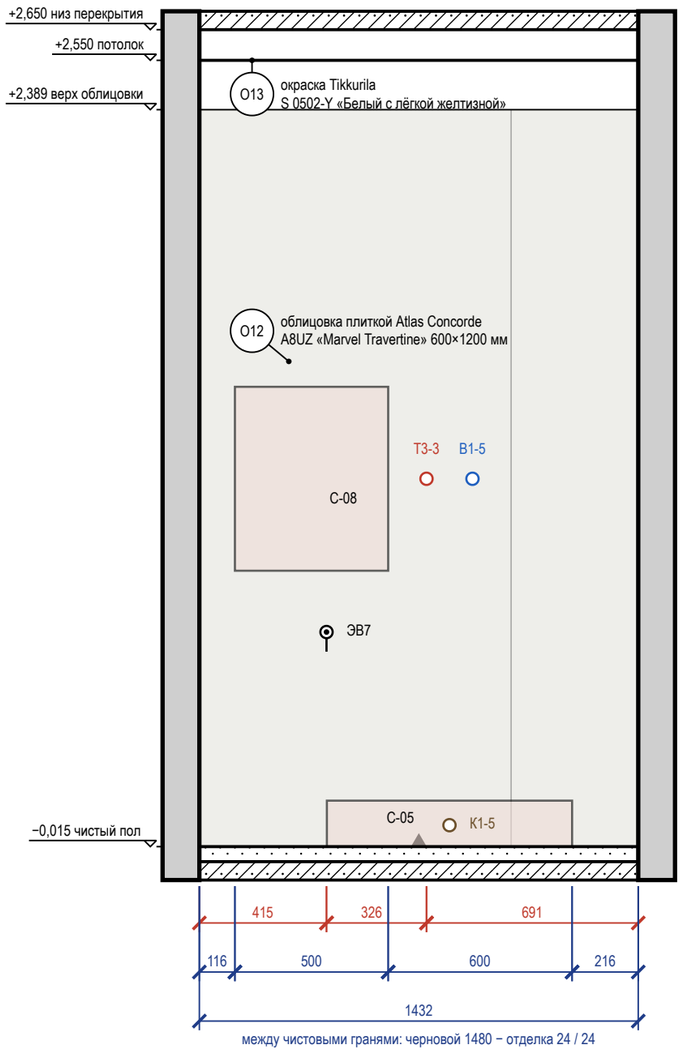

Стена Г (М 1:20)

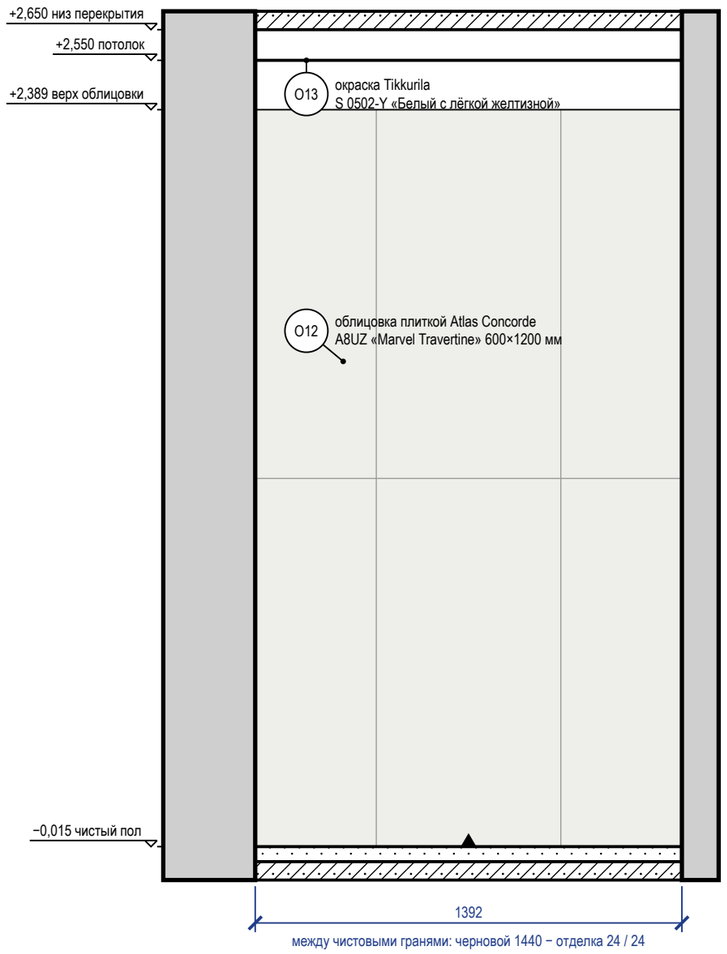


Ведомость точек и выводов

Стена	Марка	Что это	Гр.	Н, мм	От угла, мм	Примечание
В	ЭВ7	вывод кабеля: полотенцесушитель П13	7	700	415	
В	Т3-3	горячая вода — душ		1200	741	межос. 150
В	К1-5	канализация — душ		70	816	Ø50; сифон поддона
В	В1-5	холодная вода — душ		1200	891	межос. 150

Ведомость отделки (на листе)

Марка	Поверхность	Материал, изделие	Цвет, код	Кол.
О12	стены	облицовка плиткой, Atlas Concorde Marvel Travertine, 600×1200×9 мм, A8UZ, затирка CG2WA	Atlas Concorde A8UZ «Marvel Travertine»	6,8 м²
О13	потолок	окраска, Tikkurila Luja 7, матовая, подготовка Q3	NCS S 0502-Y «Белый с лёгкой желтизной»	2,1 м²

Схема развёрток (М 1:50)

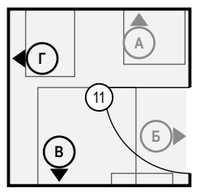

Ведомость изделий и проёмов (на листе)

Стена	Марка	Изделие, проём	На виде Ш×В, мм	Низ, мм
В	С-08	полотенцесушитель электрический 1050×500, IP44, вне зон 0–1	500×600	900
В	С-05	душ со стеклоблочной перегородкой (сохраняется)	800×150	0

Примечания

1. Размеры — в мм от чистовых поверхностей стен; условные обозначения и общие указания — лист 22.
2. Схема мебели, приборов и декора не является технической документацией для производства мебели; габариты — по паспортам изделий.
3. Выводы ВК — коды и высоты по листу выводов сантехники.
4. Облицовка — по сетке швов 2 мм, раскладка от оси стены (треугольник у пола), целые ряды от пола; подрезки — по листу раскладки плитки.
5. Гидроизоляция в 2 слоя, заход на стены 200 мм; у душа — до 2000 и 500 мм за поддон — до облицовки, с актом скрытых работ и тестом проливом (узел — на листе узлов).

	Лист	№ док.	Подпись	Дата
Дизайнер	Кырлан А.С.			14.11.26
Проверил				
Н. контр.				
Утв.				

Проект: Квартира 103 м² — **М 1:20**

Развёртки стен В, Г. Ванная мастер (пом. 11)

Стадия	Лист	Листов
П	102	129

выпуск 14.11.2026 № 32d0256903 · стр. 102 из 129

Комплект предварительный по пунктам этих таблиц. Пока по пункту нет ответа или решения, показанное на указанном листе — допущение проектировщика, а не утверждённое решение.
Сводка: открытых вопросов — 7 (из них ждут факта объекта — 4: контрольного обмера, обследования или документа); изменений в реестре — 2.

Открытые вопросы и принятые допущения

№	Формулировка	Вид	Кто решает	Если решения нет	Лист, где это проявляется
К-1	Размеры сняты со скана обмерного плана KV оформление (в см): часть подписей не читается, помещения выровнены по читаемым размерам. До заказа мебели, дверей и материалов нужен контрольный обмер.	Отсутствует Ждёт: обмера	Архитектор-планировщик	размеры на листах — по плану заказчика, уточняются по месту; мебель на заказ и материалы по ним не заказывать	л. 25 — План планировки от заказчика л. 33 — План размещения мебели и оборудования
К-2	Высота потолка принята 2650 мм по отметкам обмера (Н = 2,50…2,66 м); под ригелем 2,28 м — уточнить.	Отсутствует	Архитектор-планировщик	высоты на развёртках и потолки — от 2650 мм, уточнить при обмере	л. 25 — План планировки от заказчика л. 52 — План потолков
К-4	Разрешённая мощность объединённой квартиры по ТУ неизвестна, принята 15 кВт; при объединении двух квартир ТУ переоформляются.	Отсутствует	Инженер-электрик	щит и группы рассчитаны на 15 кВт; при меньших ТУ пересчёт	л. 56 — Однолинейная схема щита л. 59 — План розеток и электровыводов
К-5	Объединение двух квартир в одну (проём в межквартирной стене между гостиной и коридором правой квартиры, вход — один из тамбура, второй вход закрывается; правая кухня — постирочная) — предложение проектировщика. Межквартирная стена, колонны и ригель — несущие или нет, неизвестно (на обмере отмечены «несущие колонны» и «ригель перекрытия»): нужны поэтажный план БТИ, техзаключение и согласование перепланировки (ЖК РФ ст. 25–29).	Отсутствует Ждёт: документа	Архитектор-планировщик	проём и перегородки — предложение, к строительству не выдаются; мокрые зоны и кухня оставлены на местах обмера	л. 25 — План планировки от заказчика
К-6	Ванная мастер (пом. 11): стояки Ст К1-3 Ø110, Ст В1-3, Ст Т3-3 по данным стоят в углу стен В и Г (оси ≈ 90–240 мм от стены Г, 150–280 мм от стены В) — внутри габарита душевого поддона С-05 800 × 800 у стены В, а душ со стеклоблочной перегородкой по плану сохраняется. Поддон на стояки не встанет, короба (зазор 50 мм) и люка 300 × 400 к арматуре нет. Положение стояков снято со скана обмера (К-1), отдельно не замерялось. Нужен контрольный обмер угла: оси стояков от двух стен, перегородка из стеклоблоков. Затем решить: (а) короб стояков в углу ≈ 310 × 350 с люком, поддон 800 × 800 сдвинуть вдоль стены В от короба, стеклоблочную перегородку разобрать и выложить заново по новому поддону; (б) поддон меньше, вне короба (по месту после обмера); (в) душ с трапом без поддона по обходу короба.	Спорно Ждёт: обмера, затем решения	Инженер ВК (вода, канализация)	душевую зону С-05, поддон и перегородку не выполнять; выводы С-05 и короб стояков — после обмера	л. 38 — План выводов сантехники л. 39 — Схема разводки водопровода и канализации л. 25 — План планировки от заказчика

выпуск 14.11.2026 № 32d0256903 · стр. 103 из 129

	Лист	№ док.	Подпись	Дата	Проект: Квартира 103 м²			
Дизайнер	Кырлан А.С.			14.11.26	Открытые вопросы, принятые допущения и конфликты. Лист 1 из 2	Стадия	Лист	Листов
Проверил						П	103	129
Н. контр.								
Утв.								

Открытые вопросы и принятые допущения (продолжение)

№	Формулировка	Вид	Кто решает	Если решения нет	Лист, где это проявляется
К-7	Унитаз подвесной С-02 (пом. 6 «Ванная»), выпуск К1-2 Ø110: трасса до Ст К1-1 (1,91 м) идёт под дверным проёмом Д-5 — короб над полом там не поставить. Решить: (а) прибор ближе к стояку Ст К1-1 (без прохода под проёмом); (б) выпуск в полу с подъёмом пола помещения на 160 мм; (в) насосная установка (КНС) у прибора — по паспорту, требует согласования. Решение меняет санузел (высоты, раскладку плитки) — за автором с заказчиком.	Спорно Ждёт: решения	Инженер ВК (вода, канализация)	выпуск К1-2 и прибор С-02 не выполнять до решения; остальное — по листам	л. 39 — Схема разводки водопровода и канализации л. 38 — План выводов сантехники
К-8	Климатический подрайон (СП 131.13330) не задан: принят не северный — жилые комнаты и кухня под потолком от 2,5 м (СП 54, п. 5.12); в IA, IБ, IГ, IД, IVA — от 2,7 м.	Отсутствует Ждёт: документа	Архитектор-планировщик	отметки потолков жилых — по 2,5 м; при северном подрайоне уровни ниже 2,7 м пересчитать до заказа каркаса	л. 52 — План потолков

Изменения проекта после выпуска листов (реестр изменений)


№	Дата	Лист	Было	Стало	Кто решил, подпись
ИЗ-1	30.10.2026	л. 56 — Однолинейная схема щита л. 59 — План розеток и электровыводов л. 48 — Раскладка плитки. Ванная. Развёртки стен л. 50 — План размещения дверей л. С3 — Спецификация отделочных материалов л. 38 — План выводов сантехники	Фены Р8, Р33 и полотенцесушители В6, В7 сидели на гр. 13 «посудомоечная машина», стиральная машина Р50 — на гр. 12 «духовой шкаф»; групп 7 и 8 в щите не было. Два вывода печатались «ЭВ4» (духовой шкаф «ЭВ4» на кухне и вентилятор «В4» ванной). Окно 2 спальни мастер (смещение 3500, 1300) выходило за стену Б (3830). Пол ванных и плинтус МДФ — без артикула. Стояки Ст К1-3/В1-3/Т3-3 без признака допущения.	Группы 7 (санузлы: фены, полотенцесушители, УЗО 10 мА) и 8 (стиральная машина постирочной) добавлены, точки переназначены. Выводы кухни — В1 (варочная), В2 (духовой шкаф), печать ЭВ1/ЭВ2 — марки на листах уникальны. Окно 2 — стена Б части 1, смещение 100, знак «*» (К-1). Пол ванных — Marvel Travertine Sand Cross 60×60 AFUL, плинтус — Ultrawood Base 5340 83×15. Стояки ванной мастер — принято, не замерено, К-6; остаётся до обмера.	Утверждено: Кырлан А.С., 12.11.2026. Предложил: исполнитель.
ИЗ-2	10.11.2026	л. 50 — План размещения дверей л. 33 — План размещения мебели и оборудования л. 59 — План розеток и электровыводов	Д-9 (ванная мастер, стена В, 700 мм) открывалась в ванную и задевала душевой поддон С-05; розетка Р33 (фен, стена В, смещение 489 мм, высота 1000) — в зоне 2 душа: 488 мм от границы зоны 1 при норме не менее 600.	Д-9 открывается из ванной в спальню (петли у начала проёма); комод М-31 в спальне сдвинут на 120 мм (смещение 2320, было 2200): зазор от дуги полотна до комода больше 20 мм. Р33 — на стене В со смещением 180 мм (было 489), высота 1000 мм и назначение прежние: дальше от душа (зона 2 — граница зоны 1 не ближе 600 мм), в центре плитки 600 мм по горизонтали, у умывальника С-07. Душ С-05 (сохраняется, К-6) и его положение не тронуты.	Утверждено: Кырлан А.С., 12.11.2026. Предложил: исполнитель.

Примечания


1. Номера листов — по ведомости рабочих чертежей комплекта (лист «Общие данные»).
2. Графа «Если решения нет» показывает состояние решения на листах; влияние на сроки и стоимость по пунктам не оценивалось.
3. Пункт, по которому принято решение, при следующем выпуске комплекта из таблиц исключается.

	Лист	№ док.	Подпись	Дата	Проект: Квартира 103 м²			
Дизайнер	Кырлан А.С.			14.11.26	Открытые вопросы, принятые допущения и конфликты. Лист 2 из 2	Стадия	Лист	Листов
Проверил						П	104	129
Н. контр.								
Утв.								


Общий вид (М 1:20)

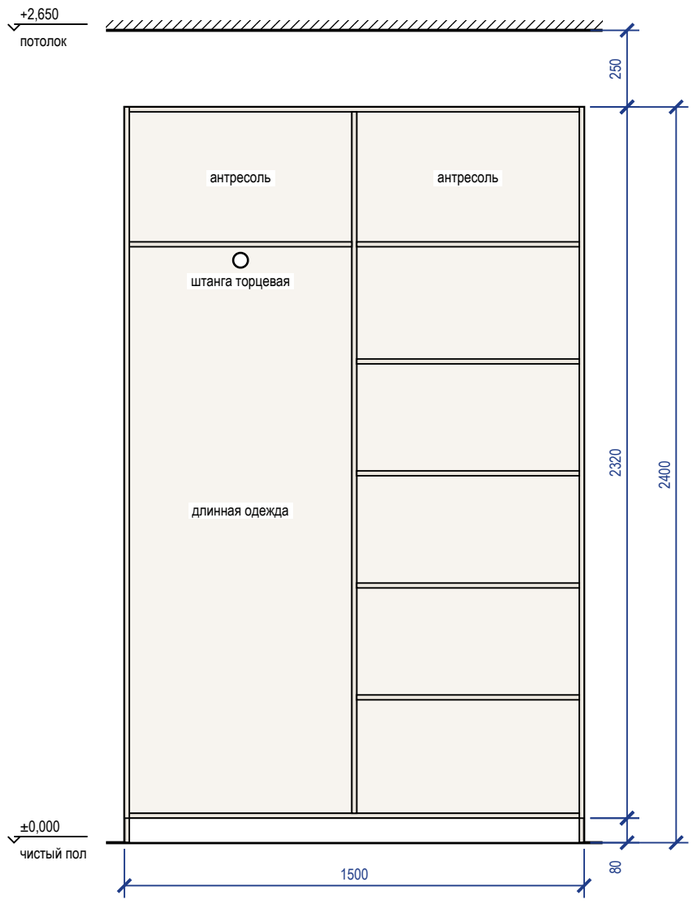


Наполнение, размеры в свету (М 1:20)

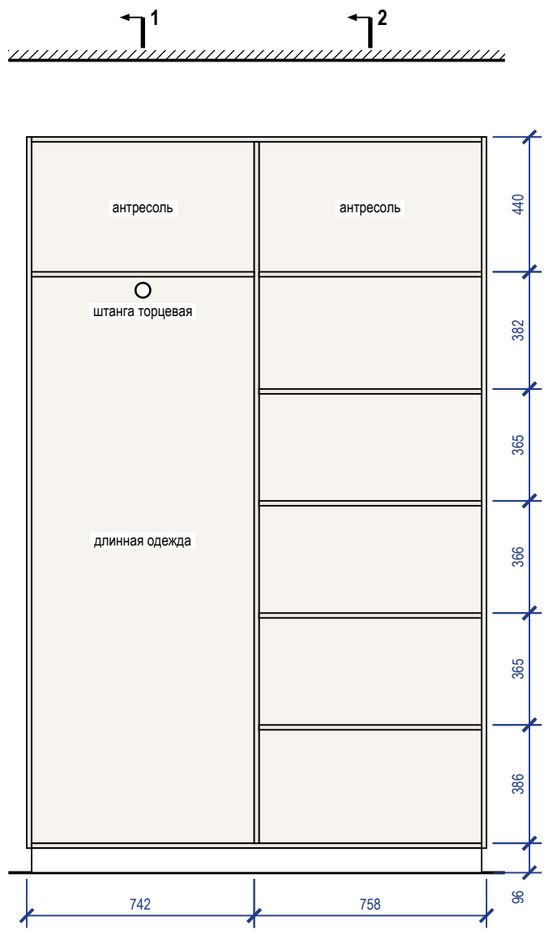

Разрез 1-1 (М 1:20)

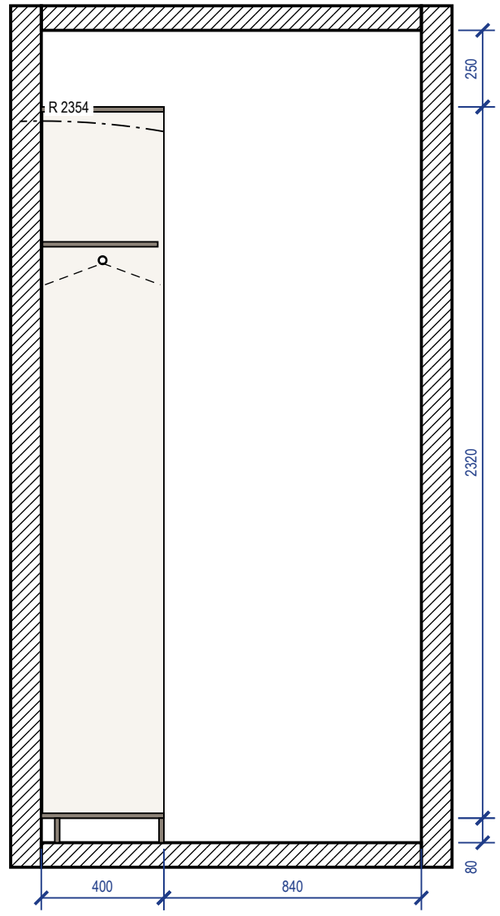


Разрез 2-2 (М 1:20)

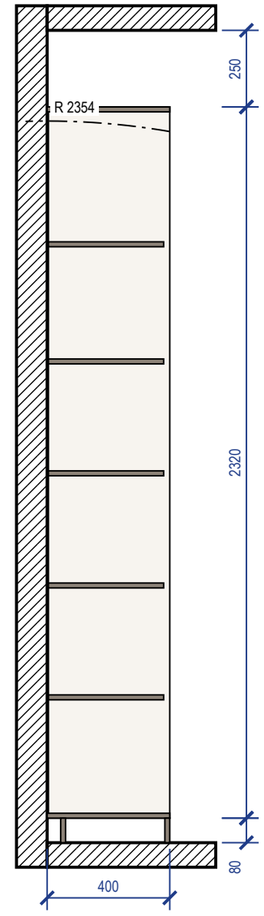

Примечания

1. Размеры — в мм по чистовой отделке; изделие 1500×400×2400 (Ш×Г×В). Перед раскроем — контрольный замер цеха после чистовой отделки стен, пола и потолка.
2. Корпус — ЛДСП декор «орех» 16 мм, задняя стенка ХДФ 4 мм в паз, цоколь 80 мм на регулируемых опорах; открытая система: без фасадов.
3. Кромка: скрытые торцы 0,4 мм, видимые 2 мм (ПВХ/АБС).
4. Присадка по 32-й системе — выполняет цех.
5. Зазор до потолка 250 мм.
6. Подъём корпуса: диагональ боковины без цоколя $\sqrt{(2320^2 + 400^2)} = 2354$ мм < 2650 мм до потолка — корпус собирается лёжа, поднимается поворотом и ставится на цоколь.
7. Крепление к стене от опрокидывания — уголки 2 шт. к несущему основанию (монтажная схема шкафов).
8. Проход перед изделием 840 мм показан на разрезе 1-1.

3D орто

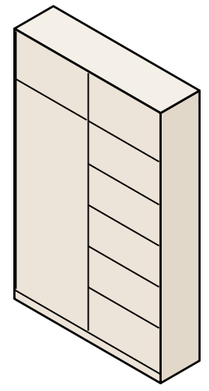


	Лист	№ док.	Подпись	Дата
Дизайнер	Кырлан А.С.			14.11.26
Проверил				
Н. контр.				
Утв.				

Проект: Квартира 103 м² — **М 1:20**


Система хранения М-05	Стадия	Лист	Листов
	П	Д1	129

выпуск 14.11.2026 № 32d0256903 · стр. 105 из 129


Вид с фасадами (М 1:40)

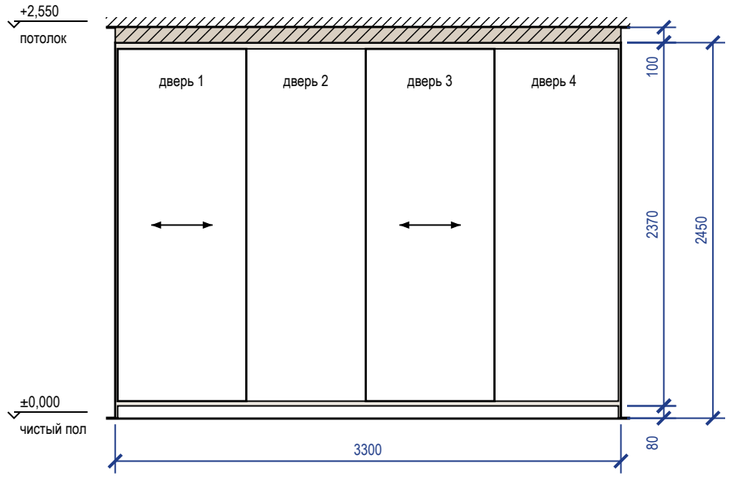


Вид без фасадов (М 1:40)

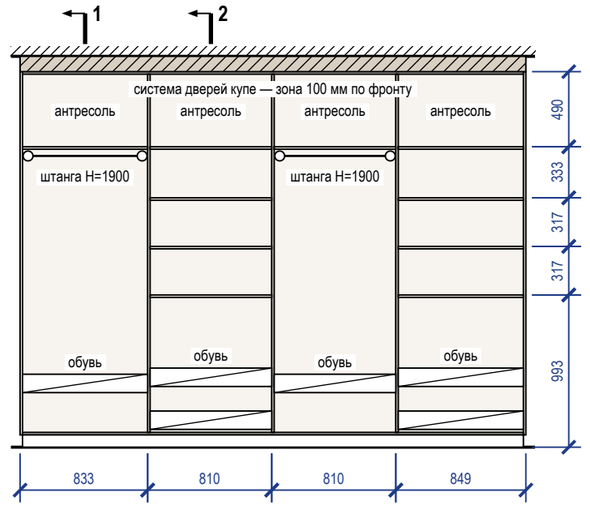

Разрез 1-1 (М 1:40)

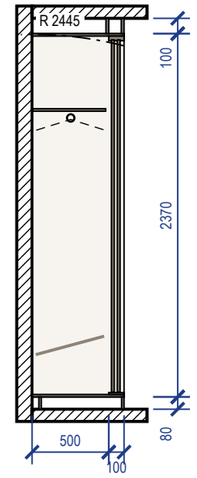

Разрез 2-2 (М 1:40)

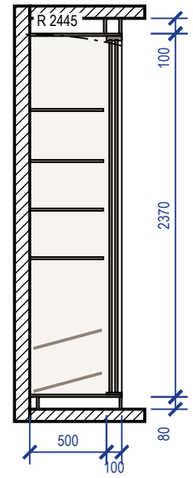

Примечания


1. Размеры — в мм по чистовой отделке; изделие 3300×600×2450 (Ш×Г×В). Перед раскроем — контрольный замер цеха после чистовой отделки стен, пола и потолка.
2. Корпус — ЛДСП 16 мм, задняя стенка ХДФ 4 мм в паз, цоколь 80 мм на регулируемых опорах; двери купе — МДФ, шпон ореха 10 мм, масло матовое в профиле: латунь; нахлёст 30 мм, ширина двери 840 мм, высота — проём минус 40 мм; цвет — по колерной карте.
3. Кромка: скрытые торцы 0,4 мм, видимые 2 мм (ПВХ/АБС).
4. Номинальные зазоры: дверь купе — боковина 3 мм, фасад ящика — стойка 2 мм; ящики внутри купе — с накладкой 30 мм на стойке со стороны нахлёста дверей.
5. Присадка по 32-й системе — выполняет цех.
6. Компенсатор 100 мм — короб из ЛДСП по фронту и торцам, подгоняется к потолку при монтаже (припуск 20 мм), крепится к корпусу и к потолку.
7. Подъём корпуса: диагональ боковины без цоколя $\sqrt{(2370^2 + 600^2)} = 2445$ мм < 2550 мм до потолка — корпус собирается лёжа, поднимается поворотом и ставится на цоколь.
8. Крепление к стене от опрокидывания — уголки 2 шт. к несущему основанию (монтажная схема шкафов).

3D орто


	Лист	№ док.	Подпись	Дата	Проект: Квартира 103 м²			М 1:40
Дизайнер	Кырлан А.С.			14.11.26	Шкаф-купе М-11	Стадия	Лист	Листов
Проверил						П	Д2	129
Н. контр.								
Утв.								

выпуск 14.11.2026 № 32d0256903 · стр. 106 из 129


Общий вид (М 1:20)

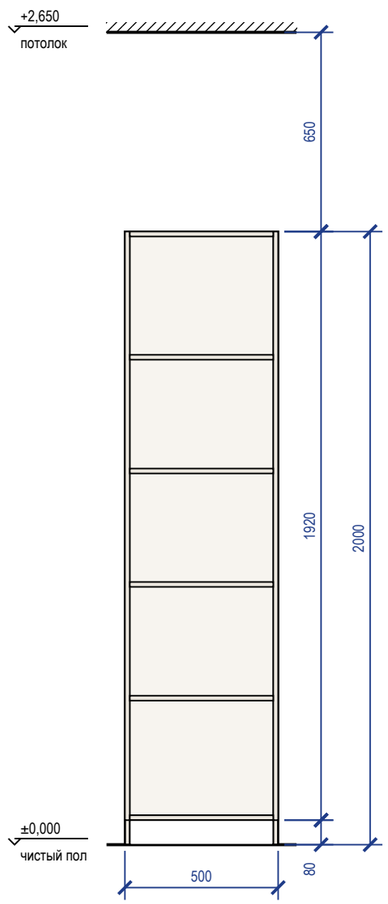

Наполнение, размеры в свету (М 1:20)

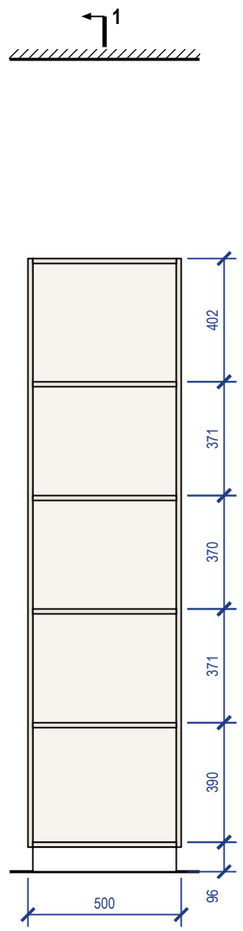


Разрез 1-1 (М 1:20)

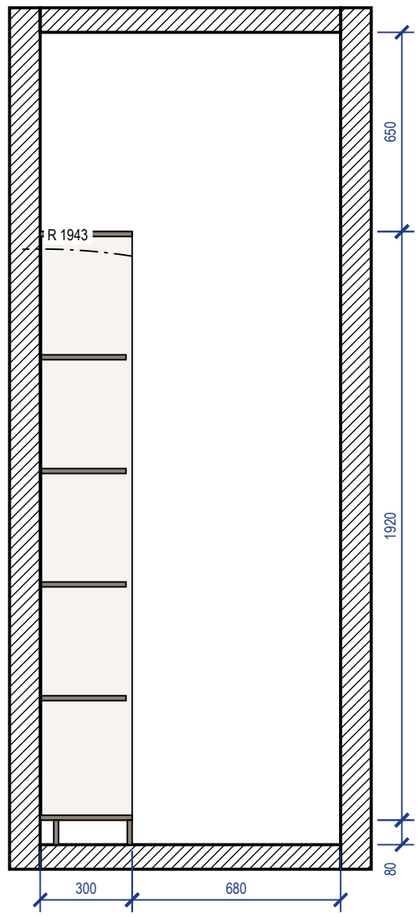

Примечания

1. Размеры — в мм по чистовой отделке; изделие 500×300×2000 (Ш×Г×В). Перед раскроем — контрольный замер цеха после чистовой отделки стен, пола и потолка.
2. Корпус — ЛДСП 16 мм, задняя стенка ХДФ 4 мм в паз, цоколь 80 мм на регулируемых опорах; открытая система: без фасадов.
3. Кромка: скрытые торцы 0,4 мм, видимые 2 мм (ПВХ/АБС).
4. Присадка по 32-й системе — выполняет цех.
5. Зазор до потолка 650 мм.
6. Подъём корпуса: диагональ боковины без цоколя $\sqrt{(1920^2 + 300^2)} = 1943$ мм < 2650 мм до потолка — корпус собирается лёжа, поднимается поворотом и ставится на цоколь.
7. Крепление к стене от опрокидывания — уголки 2 шт. к несущему основанию (монтажная схема шкафов).
8. Проход перед изделием 680 мм показан на разрезе 1-1.


3D орто

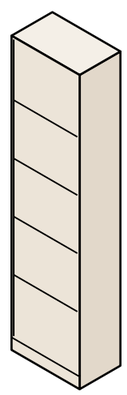


	Лист	№ док.	Подпись	Дата	Проект: Квартира 103 м²	М 1:20		
Дизайнер	Кырлан А.С.			14.11.26				
Проверил					Система хранения М-22	Стадия	Лист	Листов
Н. контр.						П	Д3	129
Утв.								

выпуск 14.11.2026 № 32d0256903 · стр. 107 из 129


Вид с фасадами (М 1:20)

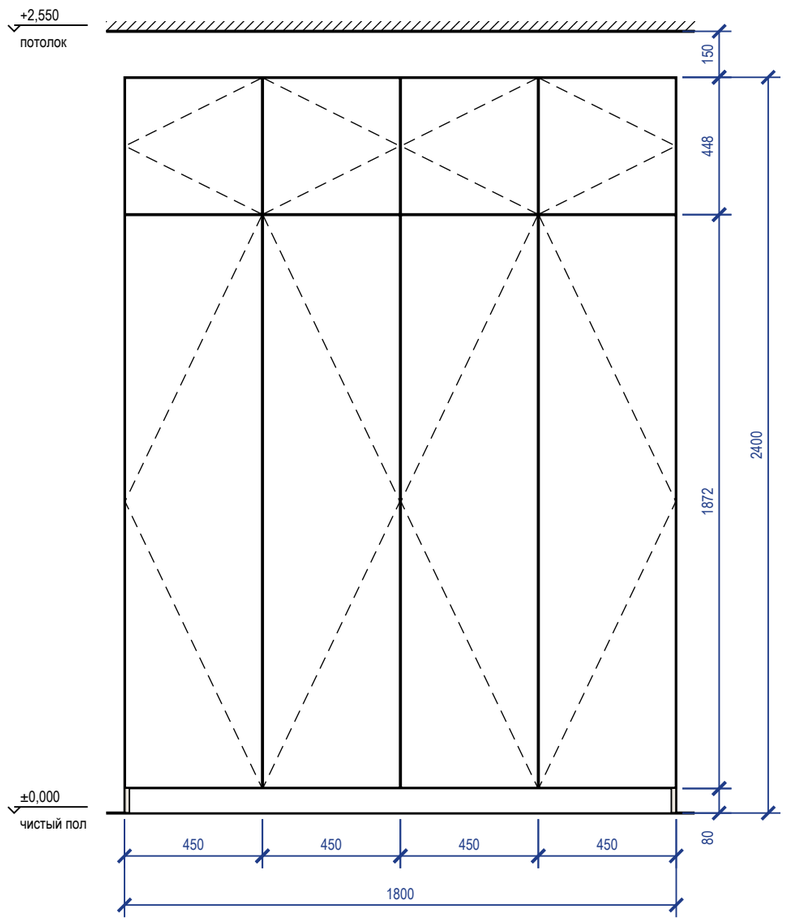


Вид без фасадов (М 1:20)

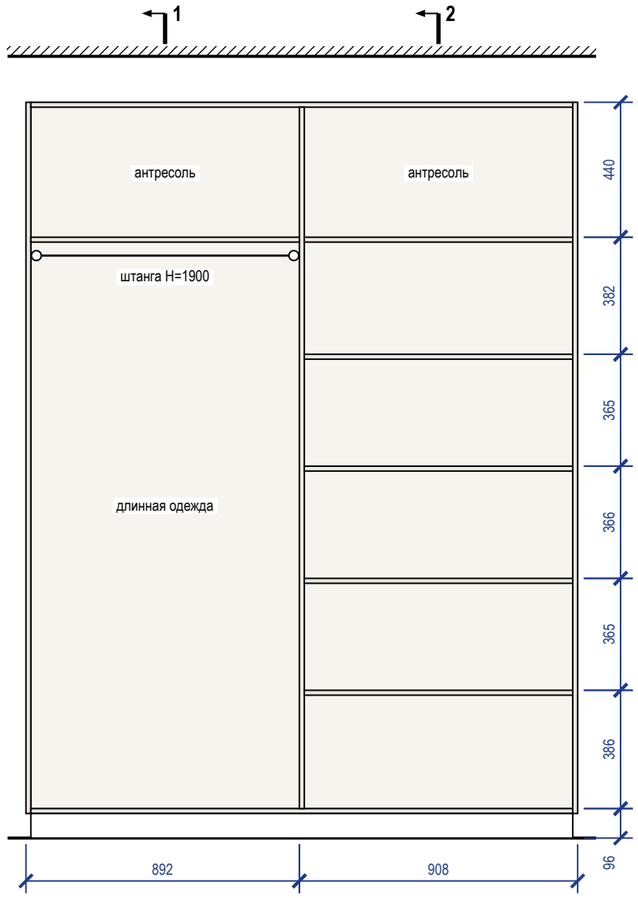

Разрез 1-1 (М 1:20)

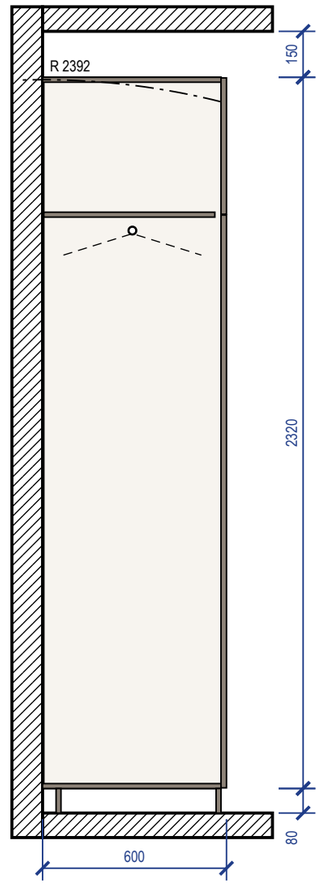


Разрез 2-2 (М 1:20)

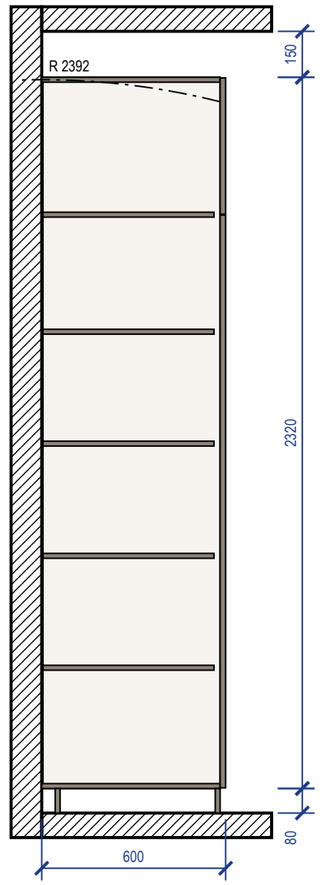

Примечания

1. Размеры — в мм по чистовой отделке; изделие 1800×600×2400 (Ш×Г×В). Перед раскроем — контрольный замер цеха после чистовой отделки стен, пола и потолка.
2. Корпус — ЛДСП 16 мм, задняя стенка ХДФ 4 мм в паз, цоколь 80 мм на регулируемых опорах; фасады накладные — МДФ, шпон ореха 18 мм, масло матовое; цвет — по колерной карте; петли с доводчиком: фасад 1869 мм — 4 петли, фасад 445 мм — 2 петли.
3. Кромка: скрытые торцы 0,4 мм, видимые 2 мм (ПВХ/АБС).
4. Номинальные зазоры: между фасадами 3 мм, фасад — стена и фасад — потолок не менее 3 мм, фасад ящика — стойка 2 мм.
5. Присадка по 32-й системе — выполняет цех.
6. Зазор до потолка 150 мм — закрыть планкой в цвет корпуса при монтаже.
7. Подъём корпуса: диагональ боковины без цоколя $\sqrt{(2320^2 + 582^2)} = 2392$ мм < 2550 мм до потолка — корпус собирается лёжа, поднимается поворотом и ставится на цоколь.
8. Крепление к стене от опрокидывания — уголки 2 шт. к несущему основанию (монтажная схема шкафов).

3D орто

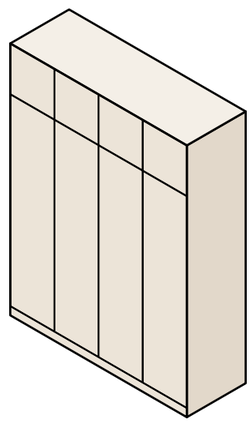


	Лист	№ док.	Подпись	Дата
Дизайнер	Кырлан А.С.			14.11.26
Проверил				
Н. контр.				
Утв.				

Проект: Квартира 103 м² — **М 1:20**


Шкаф распашной М-24	Стадия	Лист	Листов
	П	Д4	129

выпуск 14.11.2026 № 32d0256903 · стр. 108 из 129


Вид с фасадами (М 1:20)

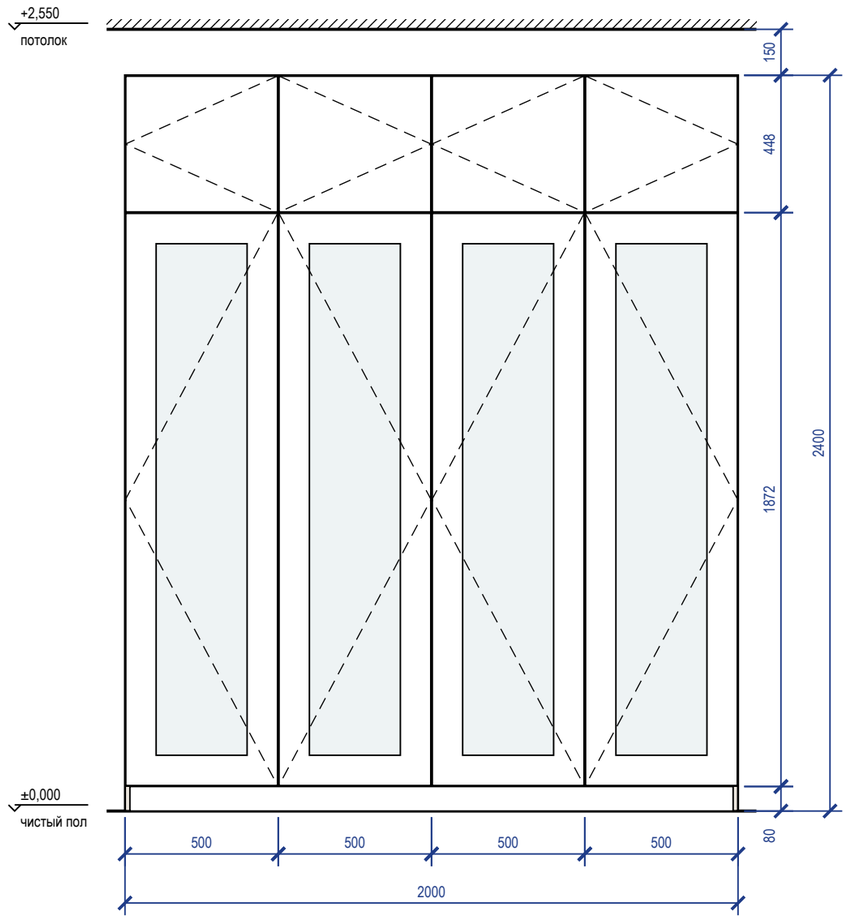


Вид без фасадов (М 1:20)

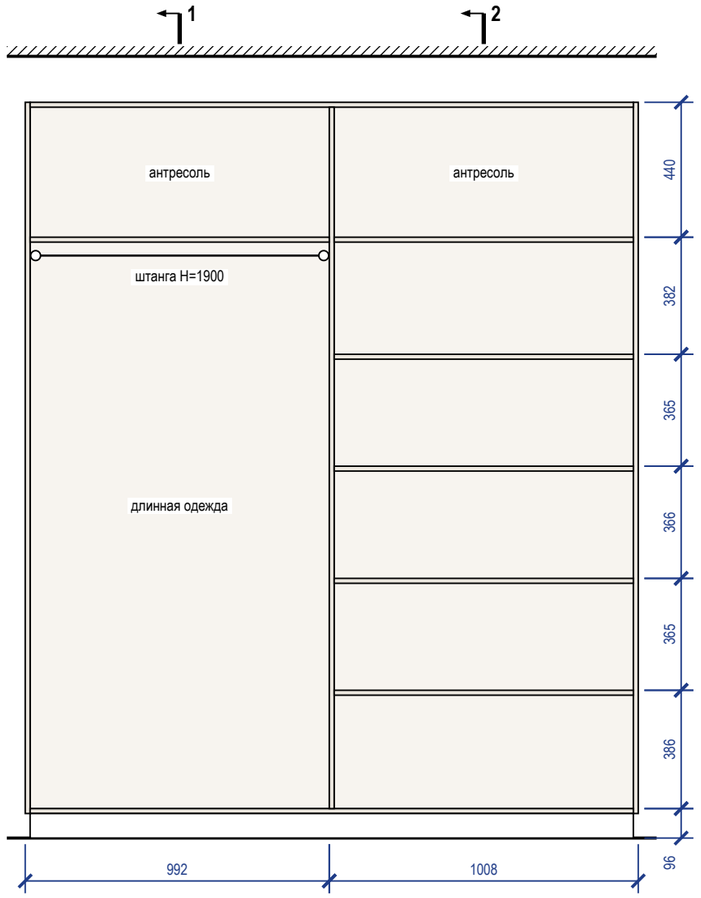

Разрез 1-1 (М 1:20)

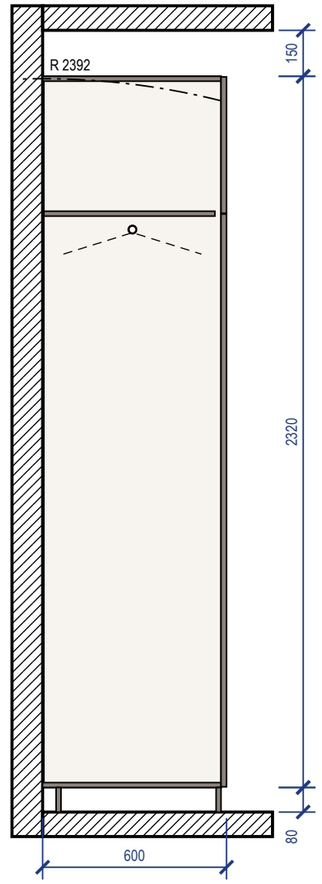


Разрез 2-2 (М 1:20)

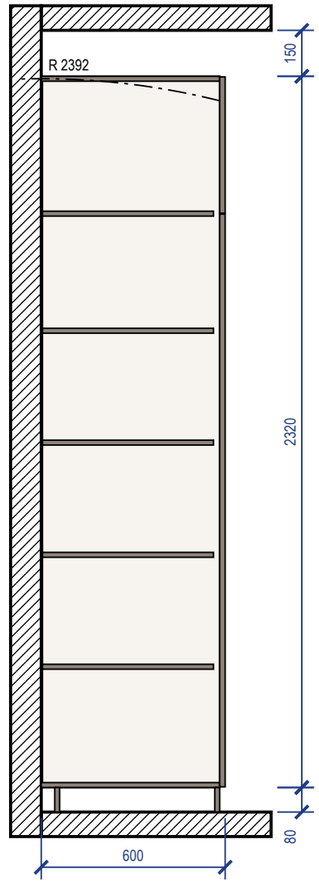

Примечания

1. Размеры — в мм по чистовой отделке; изделие 2000×600×2400 (Ш×Г×В). Перед раскроем — контрольный замер цеха после чистовой отделки стен, пола и потолка.
2. Корпус — ЛДСП 16 мм, задняя стенка ХДФ 4 мм в паз, цоколь 80 мм на регулируемых опорах; фасады накладные — МДФ, шпон ореха 18 мм, масло матовое; вставка — латунь; цвет — по колерной карте; петли с доводчиком: фасад 1869 мм — 4 петли, фасад 445 мм — 2 петли.
3. Кромка: скрытые торцы 0,4 мм, видимые 2 мм (ПВХ/АБС).
4. Номинальные зазоры: между фасадами 3 мм, фасад — стена и фасад — потолок не менее 3 мм, фасад ящика — стойка 2 мм.
5. Присадка по 32-й системе — выполняет цех.
6. Зазор до потолка 150 мм — закрыть планкой в цвет корпуса при монтаже.
7. Подъём корпуса: диагональ боковины без цоколя $\sqrt{(2320^2 + 582^2)} = 2392$ мм < 2550 мм до потолка — корпус собирается лёжа, поднимается поворотом и ставится на цоколь.
8. Крепление к стене от опрокидывания — уголки 2 шт. к несущему основанию (монтажная схема шкафов).

3D орто

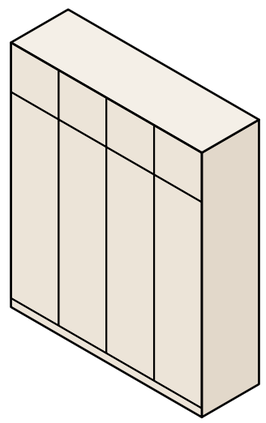


	Лист	№ док.	Подпись	Дата
Дизайнер	Кырлан А.С.			14.11.26
Проверил				
Н. контр.				
Утв.				

Проект: Квартира 103 м² — **М 1:20**


Шкаф распашной М-29	Стадия	Лист	Листов
	П	Д5	129

выпуск 14.11.2026 № 32d0256903 · стр. 109 из 129


Вид с фасадами (М 1:20)

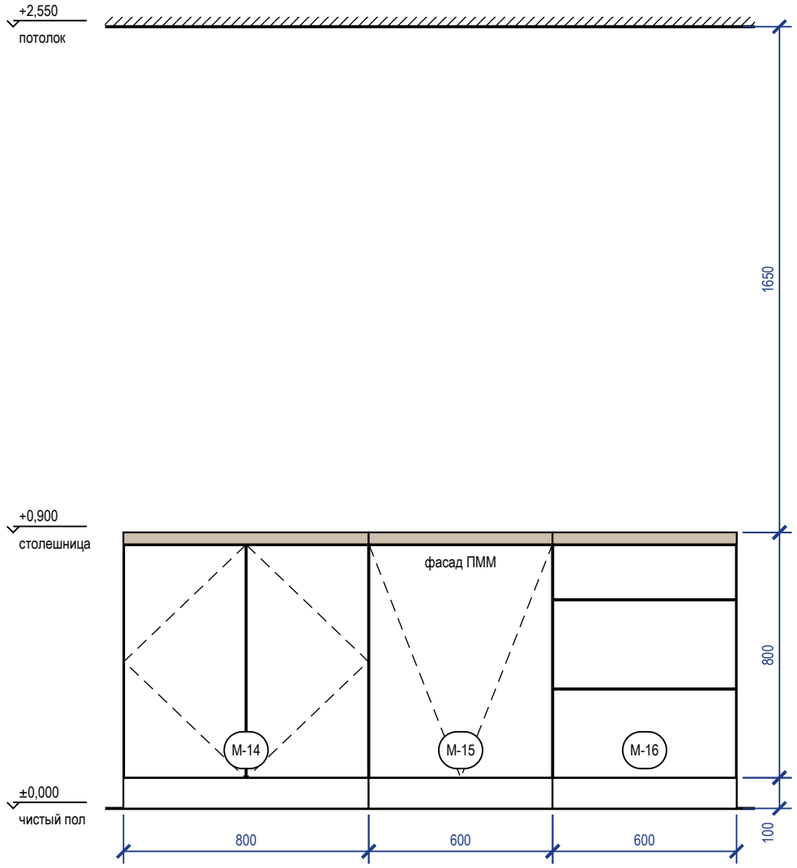


Вид без фасадов: наполнение, выводы (М 1:20)

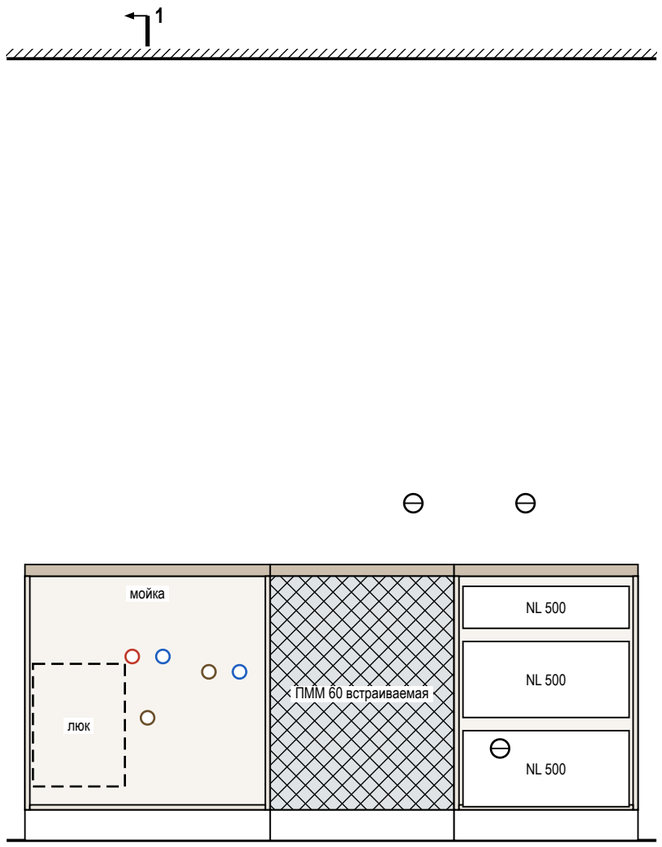

Разрез 1-1 (М 1:20)

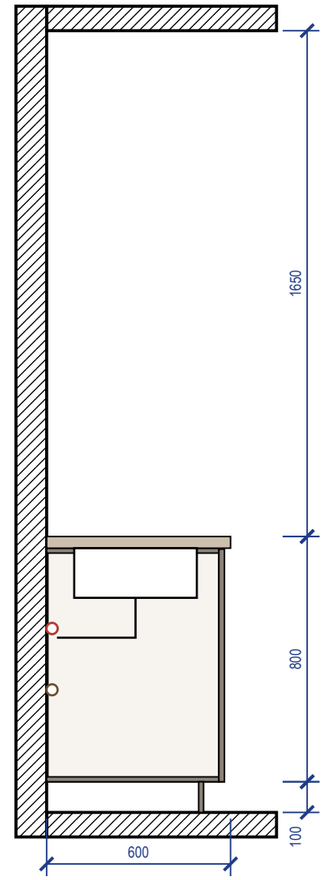

3D орто

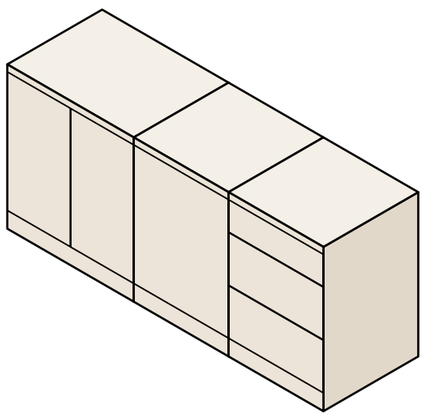


Примечания

1. Размеры — в мм по чистовой отделке, вид из помещения; марки — как на плане расстановки. Перед раскроем — контрольный замер цеха после фартука и пола.
2. Корпуса — ЛДСП 16 мм, задняя стенка ХДФ 4 мм; фасады — МДФ, шпон ореха 18 мм, цвет по колерной карте; столешница 38 мм, свес 20 мм; цоколь 100 мм.
3. Кромка: скрытые торцы 0,4 мм, видимые 2 мм. Номинальные зазоры: между фасадами 3 мм, фасад — столешница 3 мм, фасад — стена не менее 3 мм.
4. Ящики полного выдвижения и петли — с доводчиком; присадка по 32-й системе — выполняет цех.
5. Наименования и габариты модулей (М…) — в ведомости изделий, лист 37.
6. Ниши техники — по монтажным схемам выбранных моделей: решётка в цоколе и канал за пеналом холодильника, зазор за духовым шкафом, фасад ПММ на двери машины.
7. М-14: сервисный люк к стоякам Ст К1-2 (кухня), Ст В1-2, Ст Т3-2 — съёмная панель 300×400 мм в задней стенке на саморезах (по виду без фасадов, штриховой контур «люк»), доступ через фасад модуля; короб стояков за модулем — с ревизией напротив люка (лист ВК).


	Лист	№ док.	Подпись	Дата	Проект: Квартира 103 м²		М 1:20	
Дизайнер	Кырлан А.С.			14.11.26				
Проверил					Кухня (пом. 5). Развёртка гарнитура	Стадия	Лист	Листов
Н. контр.						П	Д6	129
Утв.								

выпуск 14.11.2026 № 32d0256903 · стр. 110 из 129


Вид с фасадами (М 1:20)

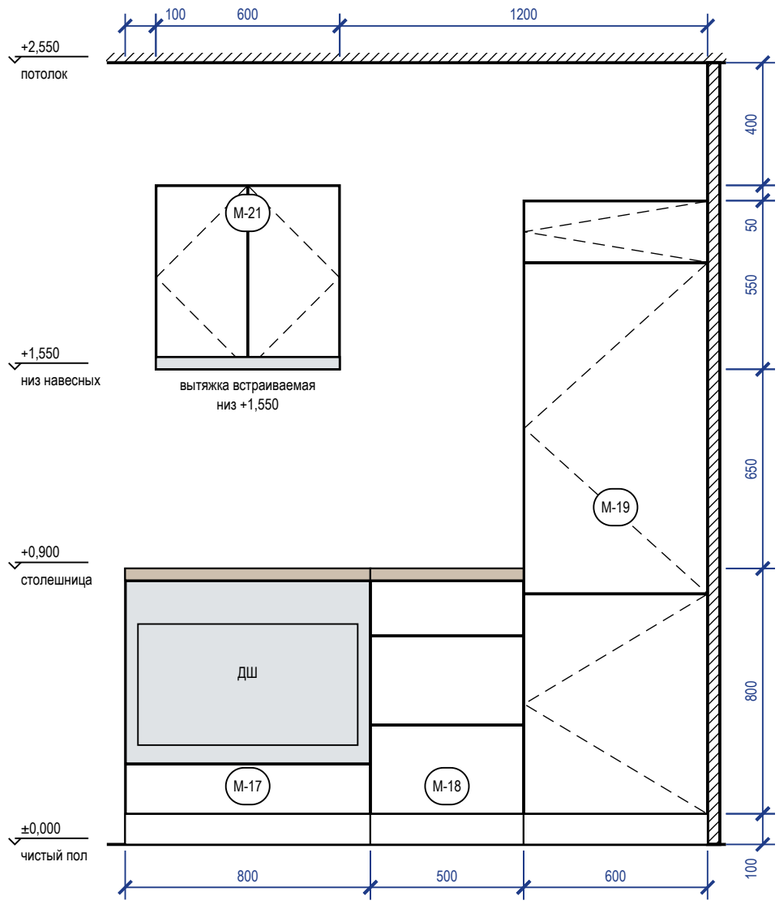


Вид без фасадов: наполнение, выводы (М 1:20)

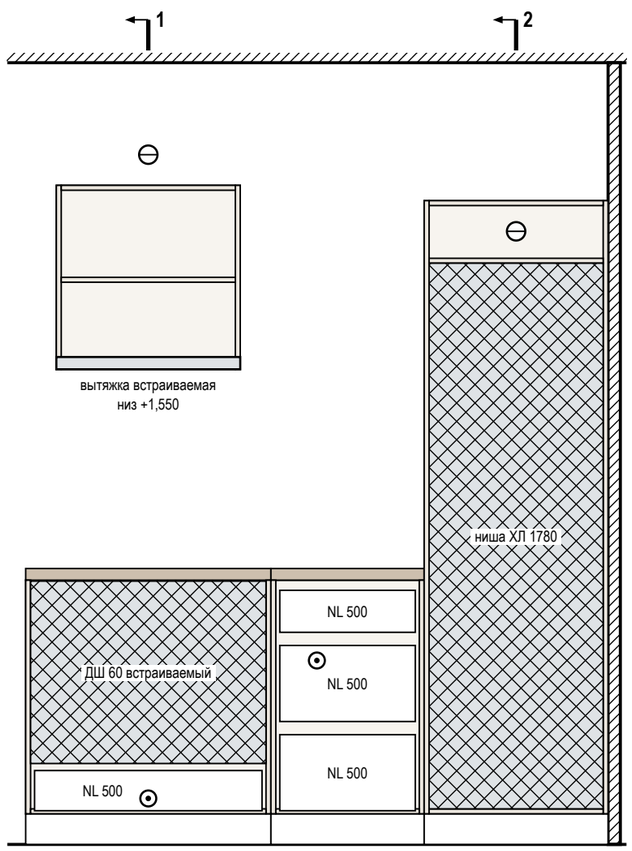


Разрез 1-1 (М 1:20)

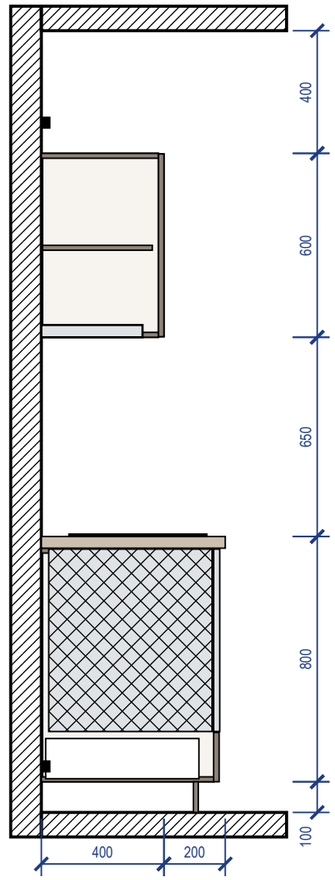

Разрез 2-2 (М 1:20)

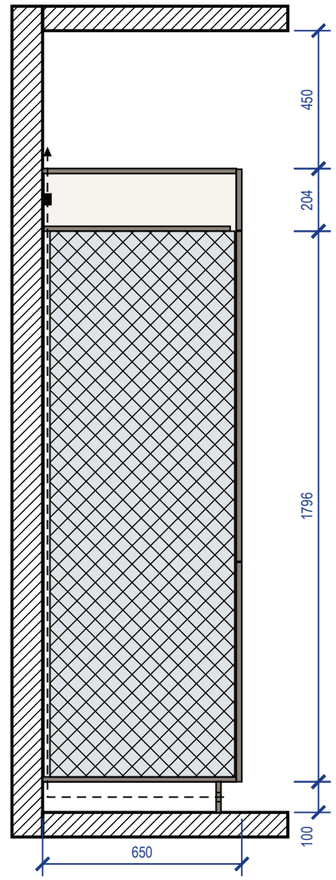

3D орто

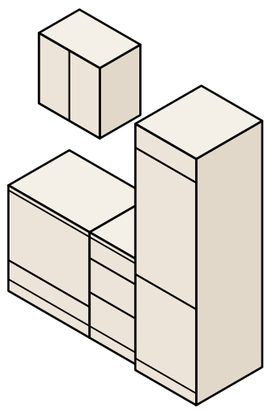

Примечания

1. Размеры — в мм по чистовой отделке, вид из помещения; марки — как на плане расстановки. Перед раскроем — контрольный замер цеха после фартука и пола.
2. Корпуса — ЛДСП 16 мм, задняя стенка ХДФ 4 мм; фасады — МДФ, эмаль матовая 18 мм, цвет по колерной карте; столешница 38 мм, свес 20 мм; цоколь 100 мм.
3. Кромка: скрытые торцы 0,4 мм, видимые 2 мм. Номинальные зазоры: между фасадами 3 мм, фасад — столешница 3 мм, фасад — стена не менее 3 мм.
4. Ящики полного выдвижения и петли — с доводчиком; присадка по 32-й системе — выполняет цех.
5. Наименования и габариты модулей (М…) — в ведомости изделий, лист 37.
6. Вытяжка встраивается в дно навесного модуля М-21 над варочной: её низ на 1550 мм от пола, 650 мм над панелью (не меньше 650 мм).
7. Ниши техники (холодильник — ориентир 1780 мм) — по монтажным схемам выбранных моделей: решётка в цоколе и канал за пеналом холодильника, зазор за духовым шкафом, фасад ПММ на двери машины.

	Лист	№ док.	Подпись	Дата	Проект: Квартира 103 м²			М 1:20
Дизайнер	Кырлан А.С.			14.11.26	Кухня (пом. 5). Развёртка гарнитура	Стадия	Лист	Листов
Проверил						П	Д7	129
Н. контр.								
Утв.								

выпуск 14.11.2026 № 32d0256903 · стр. 111 из 129

Ведомость отделки помещений (форма 1 прил. А ГОСТ 21.501-2018). Лист 1 из 2

№	Наименование помещения	Потолок			Стены и перегородки			Низ стен (плинтус)			Пол		Примечание
		Вид отделки	Код цвета	S, м²	Вид отделки	Код цвета	S, м²	Вид отделки	Код цвета	L, м	Вид отделки	S, м²	
1	Кабинет-библиотека 10,57 м²	ГКЛ по каркасу П113, отм. +2,550; окраска, Tikkurila Anti-Reflex 2, глубокоматовая, 2 слоя, подготовка Q3	NCS S 0502-Y	10,57	Окраска, Farrow & Ball Modern Emulsion, матовая, 2 слоя, подготовка Q3 Акцент — стена А: окраска, Farrow & Ball Modern Emulsion, матовая, 2 слоя, подготовка Q3	Farrow & Ball No. 291 Farrow & Ball No. 289	19,91 11,42	Плинтус МДФ h=83 мм, Ultrawood Base 5340, ЛДФ под окраску, 83×15 мм, 2440 мм (арт. LDF-BASE-5340)	Farrow & Ball No. 291	12,9	Инженерная доска, 1167-4250, 2100×127 мм, на клею; тип 1, отм. ЧП ±0,000	10,57	Н стен 2550 (до потолка); плинтус в цвет: стены
2	Кладовая 2,93 м²	Существующий потолок, отм. +2,650; окраска, Tikkurila Anti-Reflex 2, глубокоматовая, 2 слоя, подготовка Q3	NCS S 0502-Y	2,93	Окраска, Tikkurila Harmony, матовая, 2 слоя, подготовка Q3	NCS S 0502-Y	17,61	Плинтус МДФ h=83 мм, Ultrawood Base 5340, ЛДФ под окраску, 83×15 мм, 2440 мм (арт. LDF-BASE-5340)	NCS S 0502-Y	6,5	Инженерная доска, 1167-4250, 2100×127 мм, на клею; тип 1, отм. ЧП ±0,000	2,93	Н стен 2650 (до потолка); плинтус в цвет: стены
3	Гостиная-столовая 20,32 м²	ГКЛ по каркасу П113, отм. +2,550; окраска, Farrow & Ball Modern Emulsion, матовая, 2 слоя, подготовка Q3	Farrow & Ball No. 291	20,32	Окраска, Farrow & Ball Modern Emulsion, матовая, 2 слоя, подготовка К3 Акцент — стена А: окраска, Farrow & Ball Modern Emulsion, матовая, 3 слоя, аналог: интерьерная краска Farrow & Ball Modern Emulsion в цвете веера No. 255, матовая, подготовка К3	Farrow & Ball No. 291 Farrow & Ball No. 255	23,57 11,74	Плинтус МДФ h=83 мм, Ultrawood Base 5340, ЛДФ под окраску, 83×15 мм, 2440 мм (арт. LDF-BASE-5340)	Farrow & Ball No. 291	14,7	Инженерная доска, 1167-4250, 2100×127 мм, на клею; тип 2, отм. ЧП ±0,000	20,32	Н стен 2550 (до потолка); класс мокрого истирания по EN 13300 и блеск линейки Farrow & Ball Modern Emulsion — по ТУ производителя, в базе не сверены; потолок в цвет стен (No. 291) — краска бренда веера, Farrow & Ball Modern Emulsion; класс мокрого истирания по EN 13300 и блеск линейки Farrow & Ball Modern Emulsion — по ТУ производителя, в базе не сверены; колеруется в код стен, но по эмали на МДФ: сличать отдельным выкрасом на своей подложке (выкрас № 10); плинтус в цвет: стены
4	Прихожая-холл 12,91 м²	ГКЛ по каркасу П113, отм. +2,550; окраска, Tikkurila Anti-Reflex 2, глубокоматовая, 2 слоя, подготовка Q3	NCS S 0502-Y	12,91	Окраска, Farrow & Ball Modern Emulsion, матовая, 2 слоя, подготовка Q3	Farrow & Ball No. 291	33,88	Плинтус МДФ h=83 мм, Ultrawood Base 5340, ЛДФ под окраску, 83×15 мм, 2440 мм (арт. LDF-BASE-5340)	Farrow & Ball No. 291	12,6	Керамогранит, A8UZ, 600×1200×9 мм; тип 3, отм. ЧП ±0,000	12,91	Н стен 2550 (до потолка); матовая моющаяся, класс 1 EN 13300 — осознанно вместо полуматовой; плинтус в цвет: стены
5	Кухня 6,52 м²	ГКЛВ по каркасу П113, отм. +2,550; окраска, Farrow & Ball Modern Emulsion, матовая, 2 слоя, подготовка Q3	Farrow & Ball No. 291	6,52	Окраска, Farrow & Ball Modern Emulsion, матовая, 2 слоя, подготовка К3 Фартук кухни (стена Б, В): облицовка керамогранитом, аналог: керамогранит матовый, тон F497, 600×600×9 мм, клей C2 TE S1, затирка CG2WA	Farrow & Ball No. 291 #F1F1EC	20,51 2,01	Плинтус МДФ h=83 мм, Ultrawood Base 5340, ЛДФ под окраску, 83×15 мм, 2440 мм (арт. LDF-BASE-5340)	Farrow & Ball No. 291	9,4	Инженерная доска, 1167-4250, 2100×127 мм, на клею; тип 4, отм. ЧП ±0,000	6,52	Н стен 2550 (до потолка); моющаяся матовая окраска Farrow & Ball Modern Emulsion (краска бренда веера No. 291,); класс мокрого истирания по EN 13300 и блеск линейки Farrow & Ball Modern Emulsion — по ТУ производителя, в базе не сверены; категория К3 по СП 71.13330.2017, табл. 7.5; по ГКЛ каркаса П113, моющаяся окраска Farrow & Ball Modern Emulsion; Q3 класс мокрого истирания по EN 13300 и блеск линейки Farrow & Ball Modern Emulsion — по ТУ производителя, в базе не сверены; колеруется в код стен, но по эмали на МДФ: сличать отдельным выкрасом на своей подложке (выкрас № 10); плинтус в цвет: стены

Примечания

1. Ведомость продолжена на листе 2 из 2; итоги, сводка площадей и примечания — на последнем листе ведомости.

	Лист	№ док.	Подпись	Дата
Дизайнер	Кырлан А.С.			14.11.26
Проверил				
Н. контр.				
Утв.				

Проект: Квартира 103 м²

Ведомость отделки помещений. Лист 1 из 2	Стадия	Лист	Листов
	П	С1	129

выпуск 14.11.2026 № 32d0256903 · стр. 112 из 129

Ведомость отделки помещений (форма 1 прил. А ГОСТ 21.501-2018). Лист 2 из 2

№	Наименование помещения	Потолок			Стены и перегородки			Низ стен (плинтус)			Пол		Примечание
		Вид отделки	Код цвета	S, м²	Вид отделки	Код цвета	S, м²	Вид отделки	Код цвета	L, м	Вид отделки	S, м²	
6	Ванная 3,91 м²	ГКЛВ по каркасу П113, отм. +2,550; окраска, Tikkurila Luja 7, матовая, 2 слоя, подготовка Q3	NCS S 0502-Y	3,91	Облицовка плиткой, A8UZ, 600×1200×9 мм, клей C2 TE S1, затирка CG2WA	Atlas Concorde A8UZ	18,00	нет			Керамогранит, Atlas Concorde Marvel Travertine Sand CrossMatte Sensitech, арт. AFUL (той же коллекции, что стены A8UZ; тон сверить по образцу), 600×600×9 мм; тип 5, отм. ЧП −0,015	3,91	Н стен 2565 (до потолка); гидроизоляция обмазочная, 2 слоя, с заведением на стены 200 мм; над ванной — до 2000 и 300 мм за борт (по пирогу пола); тест проливом и акт скрытых работ
7	Постирочная 1,51 м²	Существующий потолок, отм. +2,650; окраска, Tikkurila Anti-Reflex 2, глубокоматовая, 2 слоя, подготовка Q3	NCS S 0502-Y	1,51	Окраска, Tikkurila Harmony, матовая, 2 слоя, подготовка Q3	NCS S 0502-Y	11,89	Плинтус МДФ h=83 мм, Ultrawood Base 5340, ЛДФ под окраску, 83×15 мм, 2440 мм (арт. LDF-BASE-5340)	NCS S 0502-Y	4,3	Инженерная доска, 1167-4250, 2100×127 мм, на клею; тип 1, отм. ЧП ±0,000	1,51	Н стен 2650 (до потолка); плинтус в цвет: стены
8	Спальня 2 11,42 м²	ГКЛ по каркасу П113, отм. +2,550; окраска, Tikkurila Anti-Reflex 2, глубокоматовая, 2 слоя, подготовка Q3	NCS S 0502-Y	11,42	Окраска, Farrow & Ball Modern Emulsion, матовая, 2 слоя, подготовка Q3 Акцент — стена А: окраска, Farrow & Ball Modern Emulsion, матовая, 2 слоя, подготовка Q3	Farrow & Ball No. 291 Farrow & Ball No. 289	20,89 12,09	Плинтус МДФ h=83 мм, Ultrawood Base 5340, ЛДФ под окраску, 83×15 мм, 2440 мм (арт. LDF-BASE-5340)	Farrow & Ball No. 291	13,6	Инженерная доска, 1167-4250, 2100×127 мм, на клею; тип 1, отм. ЧП ±0,000	11,42	Н стен 2550 (до потолка); плинтус в цвет: стены
9	Коридор 6,02 м²	ГКЛ по каркасу П113, отм. +2,550; окраска, Tikkurila Anti-Reflex 2, глубокоматовая, 2 слоя, подготовка Q3	NCS S 0502-Y	6,02	Окраска, Farrow & Ball Modern Emulsion, матовая, 2 слоя, подготовка Q3	Farrow & Ball No. 291	29,17	Плинтус МДФ h=83 мм, Ultrawood Base 5340, ЛДФ под окраску, 83×15 мм, 2440 мм (арт. LDF-BASE-5340)	Farrow & Ball No. 291	10,8	Инженерная доска, 1167-4250, 2100×127 мм, на клею; тип 1, отм. ЧП ±0,000	6,02	Н стен 2550 (до потолка); матовая моющаяся, класс 1 EN 13300 — осознанно вместо полуматовой; плинтус в цвет: стены
10	Спальня мастер 22,48 м²	ГКЛ по каркасу П113, отм. +2,550; окраска, Tikkurila Anti-Reflex 2, глубокоматовая, 2 слоя, подготовка Q3	NCS S 0502-Y	22,48	Окраска, Farrow & Ball Modern Emulsion, матовая, 2 слоя, подготовка Q3 Акцент — стена А: окраска, Farrow & Ball Modern Emulsion, матовая, 2 слоя, подготовка Q3	Farrow & Ball No. 291 Farrow & Ball No. 289	31,48 12,09	Плинтус МДФ h=83 мм, Ultrawood Base 5340, ЛДФ под окраску, 83×15 мм, 2440 мм (арт. LDF-BASE-5340)	Farrow & Ball No. 291	18,5	Инженерная доска, 1167-4250, 2100×127 мм, на клею; тип 1, отм. ЧП ±0,000	22,48	Н стен 2550 (до потолка); плинтус в цвет: стены
11	Ванная мастер 2,13 м²	ГКЛВ по каркасу П113, отм. +2,550; окраска, Tikkurila Luja 7, матовая, 2 слоя, подготовка Q3	NCS S 0502-Y	2,13	Облицовка плиткой, A8UZ, 600×1200×9 мм, клей C2 TE S1, затирка CG2WA	Atlas Concorde A8UZ	12,57	нет			Керамогранит, Atlas Concorde Marvel Travertine Sand CrossMatte Sensitech, арт. AFUL (той же коллекции, что стены A8UZ; тон сверить по образцу), 600×600×9 мм; тип 5, отм. ЧП −0,015	2,13	Н стен 2565 (до потолка); гидроизоляция обмазочная, 2 слоя, с заведением на стены 200 мм; у душа — до 2000 и 500 мм за поддон (по пирогу пола); тест проливом и акт скрытых работ
	Итого			**100,72**			**288,83**			**103,5**		**100,72**	

Примечания

1. Площади поверхностей — по чистым граням стен до отделки: стены = периметр × высоту от чистого пола помещения до низа потолка минус проёмы (облицовка плиткой — до верха облицовки); плинтус = периметр минус дверные проёмы; пол и потолок — по площади помещения. Количество плиток по раскладке. Площади помещений — с учётом всех частей помещения; откосы в площадь стен не входят.
2. Акцентные стены и фартук — отдельными строками, их площадь вычтена из основной отделки стен помещения; фартук — над нижними модулями кухни от столешницы до низа навесных шкафов, где шкафов нет — на 600 мм.
3. Плинтус — длина по периметру за вычетом дверных проёмов; примыкания к наличникам и встроенной мебели — по развёрткам.
4. Формат плитки — Ш×В×Т (ширина × высота в положении укладки × толщина), мм; на полу — вдоль стен А/В × вдоль стен Б/Г.
5. Коды цвета — по веерам производителей; колеровка каждой краски одной партией, проверка выкраса при свете D65 и при лампах проекта.
6. Уровни подготовки Q1–Q4 — система Knauf, не норма ГОСТ/СП; допуски поверхностей — по СП 71.13330.2017 (действующая редакция).
7. «аналог:» — изделие задано характеристиками, марку и артикул согласовать с заказчиком до закупки.
8. Плавающая стяжка по звукоизоляции: демпферная (кромочная) лента по контуру помещения и у стояков (СП 51.13330.2011, п. 9.11); плинтус крепится только к стене.
9. Сводка площадей по материалам, м²: потолок — NCS S 0502-Y Anti-Reflex 2 — 67,84; потолок — Farrow & Ball No. 291 Modern Emulsion — 26,84; потолок — NCS S 0502-Y Luja 7 — 6,04; стены — Farrow & Ball No. 291 Modern Emulsion — 179,41; стены — Farrow & Ball No. 289 Modern Emulsion 35,60; стены — NCS S 0502-Y Harmony — 29,50; стены — Farrow & Ball No. 255 Modern Emulsion — 11,74; стены — облицовка плиткой 600×1200×9 мм, Atlas Concorde A8UZ — 30,57; фартук — облицовка керамогранитом, #F1F1EC — 2,01.

	Лист	№ док.	Подпись	Дата	Проект: Квартира 103 м²			
Дизайнер	Кырлан А.С.			14.11.26	Ведомость отделки помещений. Лист 2 из 2	Стадия	Лист	Листов
Проверил						П	С2	129
Н. контр.								
Утв.								

выпуск 14.11.2026 № 32d0256903 · стр. 113 из 129

Поз.	Наименование и техническая характеристика	Тип, марка, обозначение документа	Код продукции	Поставщик	Ед. изм.	Кол.	Образец	Примечание
	Лакокрасочные материалы							
1	Краска интерьерная водно-дисперсионная акриловая для стен и потолков, матовая, класс мокрого истирания 1 по EN 13300, база A; цвет по вееру Farrow & Ball No. 291 «School House White — тёплый меловой белый», колеровка машинная	Farrow & Ball Modern Emulsion		Farrow & Ball	л	55		поз. К1 колерной карты; пом. 1, 3, 4, 5, 8, 9, 10; S = 206,3 м² × 2 сл. × 0,12 л/м² = 49,5 л, +10 % и 0,5 л на подкраску → ≥ 55,0 л; тара 11 × 5 л
2	Краска интерьерная водно-дисперсионная акриловая для акцентных стен, матовая, класс мокрого истирания 1 по EN 13300, база C; цвет по вееру Farrow & Ball No. 289 «Inchyra Blue — тёмный сине-серый», колеровка машинная	Farrow & Ball Modern Emulsion		Farrow & Ball	л	10		поз. К2 колерной карты; пом. 1, 8, 10; S = 35,6 м² × 2 сл. × 0,12 л/м² = 8,5 л, +10 % и 0,5 л на подкраску → ≥ 9,9 л; тара 2 × 5 л
3	Краска интерьерная водно-дисперсионная акриловая для потолков, глубокоматовая, класс мокрого истирания 2 по EN 13300, база A; цвет NCS S 0502-Y «Белый с лёгкой желтизной», колеровка машинная	Tikkurila Anti-Reflex 2		Tikkurila	л	18,9		поз. К3 колерной карты; пом. 1, 2, 4, 7, 8, 9, 10; S = 67,8 м² × 2 сл. × 0,12 л/м² = 16,3 л, +10 % и 0,5 л на подкраску → ≥ 18,4 л; тара 2 × 9 л + 1 × 0,9 л
4	Краска интерьерная водно-дисперсионная акриловая для стен, матовая, класс мокрого истирания 1 по EN 13300, база A; цвет NCS S 0502-Y «Белый с лёгкой желтизной», колеровка машинная	Tikkurila Harmony		Tikkurila	л	9		поз. К5 колерной карты; пом. 2, 7; S = 29,5 м² × 2 сл. × 0,12 л/м² = 7,1 л, +10 % и 0,5 л на подкраску → ≥ 8,3 л; тара 1 × 9 л
5	Краска интерьерная водно-дисперсионная акриловая для акцентных стен, матовая, класс мокрого истирания 1 по EN 13300, база C; цвет по вееру Farrow & Ball No. 255 «Tanner's Brown — тёмный шоколад», колеровка машинная	Farrow & Ball Modern Emulsion		Farrow & Ball	л	7,5		поз. К7 колерной карты; пом. 3; S = 11,7 м² × 3 сл. × 0,12 л/м² = 4,2 л, +10 % и 0,5 л на подкраску → ≥ 5,1 л; тара 1 × 5 л + 1 × 2,5 л
6	Краска интерьерная водно-дисперсионная акриловая для потолков, матовая, класс мокрого истирания 1 по EN 13300, база A; цвет NCS S 0502-Y «Белый с лёгкой желтизной», колеровка машинная	Tikkurila Luja 7		Tikkurila	л	2,7		поз. К9 колерной карты; пом. 6, 11; S = 6,0 м² × 2 сл. × 0,12 л/м² = 1,4 л, +10 % и 0,5 л на подкраску → ≥ 2,1 л; тара 1 × 2,7 л
7	Краска для МДФ и дерева в цвет Farrow & Ball No. 291 «School House White — тёплый меловой белый» — окраска плинтуса; блеск не ниже блеска стен	марка не задана			л	2,4		поз. К4, К8; пом. 1, 3, 4, 5, 8, 9, 10; L = 92,6 м, S = 9,1 м² × 2 сл. × 0,12 л/м² + 10 %; продукт подобрать в веере Farrow & Ball
8	Краска для МДФ и дерева в цвет NCS S 0502-Y «Белый с лёгкой желтизной» — окраска плинтуса; блеск не ниже блеска стен	марка не задана			л	0,5		поз. К6; пом. 2, 7; L = 10,8 м, S = 1,1 м² × 2 сл. × 0,12 л/м² + 10 %; продукт подобрать в веере NCS
9	Грунтовка акриловая под окраску стен и потолков — из системы производителя краски	по системе краски			м²	357		площадь окраски стен, акцентов и потолков; 1 слой перед окраской; расход — по ТУ грунтовки
	Плитка и керамогранит							
10	Atlas Concorde Marvel Travertine Sand Cross 60×60 Matte Sensitech, арт. AFUL (той же коллекции, что стены A8UZ; тон сверить по образцу), 600×600×9 мм, ректификат, водопоглощение 0,1 % (BIa), противоскольжение R10, PEI IV	Atlas Concorde Marvel Travertine Sand Cross 60×60 Matte Sensitech, арт. AFUL (той же коллекции, что стены A8UZ; тон сверить по образцу)			м²	9,36		шов 2 мм; Ванная, пол; Ванная мастер, пол; по раскладке 23 шт (S = 6,04 м²), с запасом 26 шт
11	A8UZ, 600×1200×9 мм, ректификат, водопоглощение 0,1 % (BIa), противоскольжение R10, PEI IV	A8UZ		Atlas Concorde	м²	70,56		шов 2 мм; Ванная, стены А–Г; Ванная, короб инсталляции; Ванная мастер, стены А–Г; Ванная мастер, короб инсталляции; Прихожая-холл, пол; по раскладке 86 шт (S = 45,03 м²), с запасом 98 шт
12	Керамогранит матовый, тон F497, ректификат, водопоглощение 0,5 % (BIa)	аналог по характеристикам			м²	2,22		5. Кухня, фартук; количество по площади: S = 2,01 м² + 10 %; клей и затирка — после раскладки плитки
	Напольные покрытия							
13	1167-4250, рабочий слой 4 мм, эмиссия E1, укладка на клей	1167-4250		Coswick	м²	88,3		пом. 1, 2, 3, 5, 7, 8, 9, 10; S = 82,52 м² (пол + половина стены в дверных проёмах, как в смете) + 7 %; к заказу — кратно упаковке
14	Клей для паркета и инженерной доски, эластичный (СМП / полиуретановый)	по рекомендации производителя доски			м²	83		площадь приклейки; расход и шпатель — по ТУ клея
	Погонажные изделия							
15	Ultrawood Base 5340, ЛДФ под окраску, 83×15 мм, 2440 мм (арт. LDF-BASE-5340), крепление к стене, окраска в цвет Farrow & Ball No. 291	Ultrawood Base 5340, ЛДФ под окраску, 83×15 мм, 2440 мм (арт. LDF-BASE-5340)			м	102		пом. 1, 3, 4, 5, 8, 9, 10; L = 92,6 м (периметр без дверных проёмов) + 10 % на подрезку; в штуках — по длине планки
16	Ultrawood Base 5340, ЛДФ под окраску, 83×15 мм, 2440 мм (арт. LDF-BASE-5340), крепление к стене, окраска в цвет NCS S 0502-Y	Ultrawood Base 5340, ЛДФ под окраску, 83×15 мм, 2440 мм (арт. LDF-BASE-5340)			м	12		пом. 2, 7; L = 10,8 м (периметр без дверных проёмов) + 10 % на подрезку; в штуках — по длине планки
	Смеси и материалы для облицовки							
17	Затирка для швов плитки, класс CG2WA по EN 13888	Mapei Ultracolor Plus 132		Mapei	кг	4		по раскладке (a+b)/(a·b) × шов × t × 1,6 + 10 %; в т. ч. 1,0 кг — позиции раскладки без марки
18	Клей плиточный C2 TE S1 по EN 12004, слой 5 мм	Ceresit CM 17		Ceresit	кг	321		13 меш. по 25 кг; 1,5 кг/м² на 1 мм слоя + 10 %; в т. ч. 84 кг — позиции раскладки без марки
19	Гидроизоляция обмазочная мокрых зон: пол, стены по периметру, зоны замачивания; 2 слоя с армирующей лентой в углах	аналог по характеристикам			м²	18,7		площадь по листу раскладки плитки + 10 %; расход смеси — по ТУ
20	Лента демпферная по периметру пола из плитки	аналог по характеристикам			м	27,1		периметр без дверных проёмов + 10 %

Примечания

1. Количества — из геометрии проекта: площади поверхностей по чистым граням стен до отделки (те же, что в ведомости отделки и колерной карте), плитка, клей и затирка — по раскладке плиточника; в графе «Кол.» — к заказу, с запасом.
2. Краска: расход 0,12 л/м² на слой в 2 слоя, если по ТУ не задан иной; запас 10 % и 0,5 л на подкраску каждого кода. Один код — одна партия, колеровка машинная в колеровочном центре бренда; в заказ — только после утверждения выкраса (колерная карта). Фасовка — по каталогу бренда на дату выпуска; к заказу — не меньше расчётного объёма.
3. «Аналог по характеристикам» — допускается изделие другого производителя с характеристиками не ниже указанных, по согласованию с автором проекта.
4. Графы «Код продукции» и «Масса 1 ед.» не заполнены: коды по классификатору продукции не присвоены, масса единицы до 25 кг (ГОСТ 21.110-2013).
5. Грунтовка и клей для доски указаны площадью обработки; объём — по ТУ выбранного продукта.

	Лист	№ док.	Подпись	Дата
Дизайнер	Кырлан А.С.			14.11.26
Проверил				
Н. контр.				
Утв.				

Проект: Квартира 103 м²

Спецификация отделочных материалов	Стадия	Лист	Листов
	П	С3	129

выпуск 14.11.2026 № 32d0256903 · стр. 114 из 129

Список покупок: материалы для магазина

№	Что купить	Артикул или характеристика	Нужно с запасом	Брать в магазине	Фасовка	Уточнить в магазине	Помещения	Кто покупает
Покрытия полов и облицовка								
1	Инженерная доска (дуб натуральный, рабочий слой 4 мм, эмиссия E1, прямая укладка)	1167-4250	88,3 м²	88,3 м²		уточнить в магазине: м² в упаковке	1, 2, 3, 5, 7, 8, 9, 10	по проекту
2	Клей для паркетной и инженерной доски (эластичный, по ТУ изготовителя доски)	на выбор бригады по проекту	82,52 м²			уточнить в магазине: расход и фасовку — по выбранному продукту		бригада
3	Керамогранит 600×600 мм Atlas Concorde Marvel Travertine Sand Cross 60×60 Matte Sensitech, арт. AFUL (той же коллекции, что стены A8UZ; тон сверить по образцу)	Atlas Concorde Marvel Travertine Sand Cross 60×60 Matte Sensitech, арт. AFUL (той же коллекции, что стены A8UZ; тон сверить по образцу)	26 шт	26 шт		уточнить в магазине: штук в коробке	6, 11	по проекту
4	Керамогранит 600×1200 мм A8UZ	A8UZ	95 шт	98 шт		уточнить в магазине: штук в коробке	4, 6, 11	по проекту
5	Керамогранит	по характеристике: керамогранит матовый, тон F497, 600×600×9 мм	2,21 м²	2,3 м²		уточнить в магазине: м² в коробке	5	по проекту
Сухие смеси и гидроизоляция								
6	Клей плиточный цементный класса C2 TE S1 (ГОСТ Р 56387-2018)	Ceresit CM 17 или аналог	320,8 кг	13 меш.	мешок 25 кг			по проекту
7	Затирка цементная класса CG2WA, цвет — по колерной карте	Mapei Ultracolor Plus 132 или аналог	3,97 кг	2 упак.	упак. 2 кг			по проекту
8	Гидроизоляция обмазочная полимерная, 2 слоя, лента в углах, манжеты на выводах	на выбор бригады по проекту	18,71 м²			уточнить в магазине: расход и фасовку — по выбранному продукту	6, 11	бригада
9	Лента демпферная по периметру пола из плитки	на выбор бригады по проекту	27,15 м	28 м		уточнить в магазине: фасовку		бригада
10	Смесь цементно-песчаная для стяжки М200 (50 мм, 49 мм, 47 мм, 33 мм)	на выбор бригады по проекту	5,2 м³			уточнить в магазине: расход и фасовку — по выбранному продукту		бригада
11	Смесь штукатурная гипсовая для машинного и ручного нанесения по маякам, слой до 10 мм	на выбор бригады по проекту	320,19 м²			уточнить в магазине: расход и фасовку — по выбранному продукту	1, 2, 3, 4, 5, 6, 7, 8, 9, 10, 11	бригада
Короба из ГКЛВ								
12	Лист ГКЛВ 12,5 мм, 2500 × 1200 мм, обшивка коробов в 2 слоя	на выбор бригады по проекту	7,11 м²	3 лист.	лист 3,00 м²		6, 11	бригада
13	Профиль стальной оцинкованный 27 × 28 мм: каркас коробов (стойки и направляющие)	на выбор бригады по проекту	17,16 м	6 шт	хлыст 3 м			бригада
Слаботочные сети								
14	Кабель домофона — тип по системе поставщика	на выбор бригады по проекту	4,3 м	5 м		уточнить в магазине: длину бухты		бригада
15	Кабель коаксиальный RG-6 (75 Ом) к розеткам ТВ	на выбор бригады по проекту	16,1 м	17 м		уточнить в магазине: длину бухты		бригада
16	Кабель U/UTP кат. 6 (LAN, Wi-Fi и камеры по PoE)	на выбор бригады по проекту	70,3 м	71 м		уточнить в магазине: длину бухты		бригада
17	Гофротруба Ø20 для слаботочных линий, отдельно от силовых	на выбор бригады по проекту	81,6 м	82 м		уточнить в магазине: длину бухты		бригада
18	Розетка компьютерная RJ45, кат. 6, с рамкой и подрозетником	на выбор бригады по проекту	4 шт	4 шт	шт			бригада
19	Розетка телевизионная (коаксиальная) с рамкой и подрозетником	на выбор бригады по проекту	1 шт	1 шт	шт			бригада

	Лист	№ док.	Подпись	Дата	Проект: Квартира 103 м²			
Дизайнер	Кырлан А.С.			14.11.26				
Проверил					Список покупок	Стадия	Лист	Листов
Н. контр.						П	С4	129
Утв.								

выпуск 14.11.2026 № 32d0256903 · стр. 115 из 129

Список покупок: материалы для магазина (продолжение)

№	Что купить	Артикул или характеристика	Нужно с запасом	Брать в магазине	Фасовка	Уточнить в магазине	Помещения	Кто покупает
20	Трубка или монитор домофона (поставка домофонной организации)	на выбор бригады по проекту	1 шт	1 шт	шт			по проекту
21	Щит слаботочный ЩС: корпус, DIN-рейка, розетки 220 В	на выбор бригады по проекту	1 шт	1 шт	шт			бригада
22	Патч-панель, портов не менее 5	на выбор бригады по проекту	1 шт	1 шт	шт			бригада
Лакокрасочные материалы								
23	Краска интерьерная акриловая, матовая, класс истирания 1	Farrow & Ball Modern Emulsion No. 289 «Inchyra Blue — тёмный сине-серый»	9,39 л	4 банк.	банка 2,5 л		1, 8, 10	по проекту
24	Краска интерьерная акриловая, матовая, класс истирания 1	Farrow & Ball Modern Emulsion No. 291 «School House White тёплый меловой белый»	54,98 л	22 банк.	банка 2,5 л		1, 3, 4, 5, 8, 9, 10	по проекту
25	Краска интерьерная акриловая, глубокоматовая, класс истирания 2	Tikkurila Anti-Reflex 2 S 0502-Y «Белый с лёгкой желтизной»	17,91 л	7 банк.	банка 2,7 л		1, 2, 4, 7, 8, 9, 10	по проекту
26	Краска интерьерная акриловая, матовая, класс истирания 1	Tikkurila Harmony S 0502-Y «Белый с лёгкой желтизной»	7,79 л	3 банк.	банка 2,7 л		2, 7	по проекту
27	Краска интерьерная акриловая, матовая, класс истирания 1	Farrow & Ball Modern Emulsion No. 255 «Tanner's Brown — тёмный шоколад»	4,65 л	2 банк.	банка 2,5 л		3	по проекту
28	Краска интерьерная акриловая, матовая, класс истирания 1	Tikkurila Luja 7 S 0502-Y «Белый с лёгкой желтизной»	1,6 л	1 банк.	банка 2,7 л		6, 11	по проекту
29	Шпаклёвка финишная полимерная под окраску (стены и потолки, Q3)	на выбор бригады по проекту	394,88 м²			уточнить в магазине: расход и фасовку — по выбранному продукту		бригада
30	Грунтовка акриловая глубокого проникновения, 2 слоя	на выбор бригады по проекту	430,98 м²			уточнить в магазине: расход и фасовку — по выбранному продукту		бригада
Погонажные изделия и потолки								
31	Плинтус напольный МДФ под покраску, h=83 мм, крепление к стене	Ultrawood Base 5340, ЛДФ под окраску, 83×15 мм, 2440 мм (арт. LDF-BASE-5340)	113,83 м.п.	48 шт	хлыст 2,4 м		1, 2, 3, 4, 5, 7, 8, 9, 10	по проекту
32	Потолок подвесной ГКЛ/ГКЛВ по каркасу Knauf П113: листы, профили, подвесы, лента, шпаклёвка швов	Knauf П113	96,28 м²		комплект	уточнить в магазине: расход и фасовку — по выбранному продукту		по проекту

Примечания

1. «Нужно с запасом» — расход по чертежам и раскладке плюс запас на подрезку и подкраску; «Брать в магазине» — то же количество в единицах, которыми продают (банки, мешки, упаковки, листы, штуки, литры).
2. «Уточнить в магазине» — фасовки этого товара в проекте нет: спросите у продавца, сколько в упаковке, и возьмите целое число упаковок не меньше «Нужно с запасом».
3. Плитку, доску и краску одного цвета берите одной партией (один калибр и тон на помещение) и сохраните чек и номер партии до конца ремонта.
4. «По характеристике» — артикул не выбран: подойдёт любой товар с этими свойствами, согласуйте его с дизайнером до покупки. «Бригада» материал выбирает и закупает бригада по своей технологии.
5. Помещения: 1 — Кабинет-библиотека; 2 — Кладовая; 3 — Гостиная-столовая; 4 — Прихожая-холл; 5 — Кухня; 6 — Ванная; 7 — Постирочная; 8 Спальня 2; 9 — Коридор; 10 — Спальня мастер; 11 — Ванная мастер; «—» — материал для нескольких помещений, расход по месту.

	Лист	№ док.	Подпись	Дата	Проект: Квартира 103 м²			
Дизайнер	Кырлан А.С.			14.11.26	Список покупок (окончание)	Стадия	Лист	Листов
Проверил						П	С5	129
Н. контр.								
Утв.								

Смета проекта: весь проект по категориям (прайсы собраны 21.09.2026, часть расценок сверена повторно 08.11.2026)

Категория	Позиций	С ценой	По КП	Сумма по позициям с ценой, ₽
Ремонт: работы	51	33	18	1 375 189
Ремонт: материалы отделки и черновые	32	13	19	910 520
Электрика: кабель, механизмы, щит	41	0	41	
Сантехника: приборы, трубы, арматура	38	0	38	
Доставка и услуги	4	1	3	91 052
Мебель (включая кухню)	27	0	27	
Свет: светильники и ленты	61	0	61	
Техника	6	0	6	
Декор и текстиль	48	0	48	
ИТОГО по позициям с ценой (цены — нижняя граница открытых прайсов)	**308**	**47**	**261**	**2 376 761**
Резерв на непредвиденные работы и материалы, 15 % от ремонта				356 514
ВЕСЬ ПРОЕКТ — вилка «от … до …», ₽				**2 376 761 … 2 733 275**
Позиции «по КП» — цена не названа, в итог НЕ входят: работы — 18; материалы отделки и черновые — 19; электрика: кабель, механизмы, щит — 41; сантехника: приборы, трубы, арматура — 38; доставка и услуги — 3; мебель (включая кухню) — 27; свет: светильники и ленты — 61; техника — 6; декор и текстиль — 48			**261**	**итог выше на их цену**

По этапам

Этап	Поз.	С ценой	Сумма, ₽
Демонтаж и черновые работы (работы)	10	5	364 151
Инженерные системы (работы)	23	12	201 559
Чистовые работы (работы)	18	16	809 479
Черновые материалы (смеси, ГКЛ, гидроизоляция)	12	2	25 400
Электрика: кабель, механизмы, щит, слаботочка	41	0	
Сантехника: приборы, трубы, арматура	38	0	
Чистовые материалы (отделка, двери)	20	11	885 120
Доставка и услуги	4	1	91 052
Резерв на непредвиденное, 15 %	1	1	356 514
Итого ремонт (с резервом)			**2 733 275**

По помещениям

Помещение	Работы, ₽	Материалы, ₽	Всего, ₽
Общее по объекту (без привязки к помещению)	50 984		50 984
1. Кабинет-библиотека	133 522	84 255	217 777
2. Кладовая	51 488	22 810	74 298
3. Гостиная-столовая	191 801	126 485	318 286
4. Прихожая-холл	150 408	97 543	247 951
5. Кухня	99 370	41 673	141 043
6. Ванная	119 263	133 413	252 676
7. Постирочная	36 778	13 026	49 804
8. Спальня 2	143 876	90 177	234 053
9. Коридор	90 816	52 908	143 724
10. Спальня мастер	224 760	157 775	382 535
11. Ванная мастер	82 123	90 455	172 578
Доставка и услуги			91 052
Резерв 15 %			356 514
Итого ремонт (с резервом)			**2 733 275**

	Лист	№ док.	Подпись	Дата	Проект: Квартира 103 м²			
Дизайнер	Кырлан А.С.			14.11.26				
Проверил					Смета проекта: этапы, помещения, итог	Стадия	Лист	Листов
Н. контр.						П	С6	129
Утв.								

Работы по этапам с расценками (ориентир)

№	Работа	Ед.	Объём	Расценка, ₽	Сумма, ₽	Расценка	Чей подряд
1. Демонтаж и черновые работы — работы, ориентир по открытым прайсам							
1	Демонтаж существующего покрытия пола до основания	м²	100,72	по КП			бригада
2	Демонтаж существующей отделки стен до основания	м²	291,08	по КП			бригада
3	Демонтаж существующей отделки потолка до основания	м²	100,72	по КП			бригада
4	Демонтаж существующих дверных блоков	шт	9,00	по КП			бригада
5	Демонтаж существующих сантехприборов и электрооборудования (если есть)	компл		по КП			бригада
6	Устройство стяжки: стяжка ЦПС М200, 50 мм	м²	101,85	530	53 981	Ц1	бригада
7	Гидроизоляция обмазочная, 2 слоя: пол, стены на 200 мм, зоны замачивания	м²	17,01	450	7 655	Ц1	бригада
8	Штукатурка стен по маякам, до 10 мм	м²	291,08	530	154 272	Ц1	бригада
9	Штукатурка оконных откосов шириной более 200 мм	м²	7,08	540	3 823	Ц4	бригада
10	Потолок ГКЛ по каркасу П113, 1 слой	м²	96,28	1 500	144 420	Ц1	бригада
2. Инженерные системы — работы, ориентир по открытым прайсам							
11	Прокладка кабеля ВВГнг(А)-LS по группам щита: за потолком и в штробах стен (штробы — только после технического заключения, см. строку «Штробы в стенах»)	м	595,50	60	35 730	Ц3	бригада
12	Прокладка слаботочной линии: Кабель домофона — тип по системе поставщика, отдельно от силовых	м	4,30	по КП			бригада
13	Прокладка слаботочной линии: Кабель коаксиальный RG-6 (75 Ом) к розеткам ТВ, отдельно от силовых	м	16,10	по КП			бригада
14	Прокладка слаботочной линии: Кабель U/UTP кат. 6 (LAN, Wi-Fi и камеры по PoE), отдельно от силовых	м	70,30	по КП			бригада
15	Прокладка гофротрубы Ø20 для слаботочных линий, отдельно от силовых	м	81,60	140	11 424	Ц3	бригада
16	Сборка слаботочного щита ЩС: корпус, патч-панель, подключение линий и питания 220 В; коммутатор и точки доступа — оборудование заказчика	шт	1,00	по КП			бригада
17	Электроточка: подрозетник в бетоне, розетка, выключатель, вывод	шт	62,00	950	58 900	Ц3	бригада
18	Штробы в стенах под спуски кабеля к точкам — выполняются только после технического заключения о несущих стенах	м	103,59	по КП			бригада
19	Установка встраиваемого точечного светильника	шт	46,00	750	34 500	Ц3	бригада
20	Монтаж светильника: потолочного, подвесного, настенного	шт	8,00	1 200	9 600	Ц3	бригада
21	Монтаж LED-ленты в алюминиевый профиль	м	48,50	230	11 155	Ц3	бригада
22	Установка блока питания LED в доступном месте (люк, шкаф)	шт	6,00	570	3 420	Ц3	бригада
23	Установка автономного пожарного извещателя	шт	7,00	по КП			бригада
24	Сборка щита: установка автоматов и АВДТ групп, вводного автомата	шт	15,00	230	3 450	Ц3	бригада
25	Установка вводного УЗО	шт	1,00	380	380	Ц3	бригада
26	Монтаж инсталляции, установка подвесного унитаза и кнопки смыва	шт	2,00	10 500	21 000	Ц1	бригада
27	Короб инсталляции: каркас и обшивка ГКЛВ в 2 слоя, ревизионный доступ к смыву	шт	2,00	по КП			бригада
28	Короб К1 над чистым полом: каркас и обшивка ГКЛВ под плитку (материалы — в спецификации ВК)	м	7,07	по КП			бригада
29	Установка ванны с сифоном	шт	1,00	6 000	6 000	Ц1	бригада
30	Установка умывальника (мойки) с сифоном и смесителем	шт	2,00	3 000	6 000	Ц1	бригада
31	Установка душевого поддона с трапом, ограждения	шт	1,00	по КП			бригада

	Лист	№ док.	Подпись	Дата	Проект: Квартира 103 м²			
Дизайнер	Кырлан А.С.			14.11.26	Смета проекта: этапы, помещения, итог (продолжение)	Стадия	Лист	Листов
Проверил						П	С7	129
Н. контр.								
Утв.								

Работы по этапам с расценками (ориентир) (продолжение)

№	Работа	Ед.	Объём	Расценка, ₽	Сумма, ₽	Расценка	Чей подряд
32	Подключение стиральной (посудомоечной) машины к ВК	шт	1,00	по КП			бригада
33	Установка радиатора с узлом подключения и терморегулятором	шт	7,00	по КП			бригада
3. Чистовые работы — работы, ориентир по открытым прайсам							
34	Облицовка стен керамогранитом 600×1200 на клею	м²	28,89	2 500	72 225	Ц5	бригада
35	Облицовка короба инсталляции (ГКЛВ) керамогранитом: лицо, боковины, полка	м²	3,23	2 500	8 075	Ц5	бригада
36	Укладка керамогранита на пол, 600×1200, на клею	м²	19,34	1 800	34 812	Ц2	бригада
37	Затирка швов керамогранита	м²	51,07	150	7 661	Ц2	бригада
38	Грунтование стен, 2 слоя (под штукатурку и под отделку)	м²	291,08	96	27 944	Ц4	бригада
39	Шпаклёвка стен под окраску, 2 слоя (старт и финиш), уровень Q3	м²	258,26	750	193 695	Ц1	бригада
40	Грунтование и шпаклёвка оконных откосов, 2 слоя	м	30,81	300	9 243	Ц4	бригада
41	Грунтование потолка, 2 слоя	м²	100,72	96	9 669	Ц4	бригада
42	Шпаклёвка потолка под окраску, 2 слоя, уровень Q3	м²	100,72	950	95 684	Ц1	бригада
43	Окраска потолка водно-дисперсионной краской, 2 слоя	м²	100,72	360	36 259	Ц1	бригада
44	Окраска стен водно-дисперсионной краской, 2 слоя	м²	306,31	300	91 893	Ц1	бригада
45	Окраска оконных откосов, 2 слоя	м	30,81	120	3 697	Ц4	бригада
46	Укладка инженерной доски на клей	м²	82,51	1 200	99 012	Ц1	бригада
47	Установка плинтуса МДФ h=83 мм	м	103,48	450	46 566	Ц1	бригада
48	Окраска плинтуса в тоне No. 291, 2 слоя	м	103,48	300	31 044	Ц1	бригада
49	Монтаж дверей скрытого монтажа под покраску (поставщик дверей)	шт	8,00	5 250	42 000	Ц1	поставщик
50	Входная дверь, поставка с монтажом и откосами	шт	1,00	по КП			поставщик
51	Монтаж телевизора ОБ-01 на кронштейн, скрытая прокладка HDMI и питания (штроба, трубка), подключение акустики	шт	1,00	по КП			бригада
4. Прочие работы и услуги — работы, ориентир по открытым прайсам							
52	Кухонный гарнитур по проекту кухни, изготовление и монтаж (4–8 нед.)	компл	1,00	по КП			поставщик
	Итого работы (позиции с расценкой)				**1 375 189**		

Примечания

1. Итог «ВЕСЬ ПРОЕКТ» — не прогноз, а сумма того, у чего есть цена: ремонт (работы и материалы по смете сметчика), мебель, свет, техника и декор — по ценам из данных проекта. Позиции без цены названы «по КП» (261 шт.) и в итог не входят: пока цена не названа, итог выше напечатанного.
2. Вилка: «от» — сумма по позициям с ценой по нижней границе открытых прайсов (прайсы собраны 21.09.2026, часть расценок сверена повторно 08.11.2026, Москва); «до» — «от» плюс резерв на непредвиденное (15 % от ремонта; частный ремонт 10–20 %).
3. Работы — ориентир по прайсам подрядчиков, не договорная цена: расценку называет бригада после контрольного обмера. Материалы — по «Смете материалов с ценами» (следующий лист).
4. Разбивка по помещениям — доли: общая закупка делится пропорционально площади (длине, числу), по которой считается позиция; работы — по объёму строки в помещении. Сумма по помещениям, по этапам и по категориям одна и та же.
5. Источники расценок и цен: Ц1 — Домашний мастерок: прайс на отделочные работы, 2026; Ц2 — Домашний мастерок: прайс на плиточные работы, 2026; Ц3 — Домашний мастерок: прайс на электромонтажные работы, 2026; Ц4 — Профи ремонтник: штукатурно-малярные работы; Ц5 — Profi.ru: укладка керамогранита на стены, Москва 2026; Ц6 — справочник материалов: ориентир по сегментам; Ц7 — Розница Москвы, 09.2026: Лемана ПРО, KGSnab, официальный дилер Farrow & Ball.
6. Оборудование «по КП» из сметы сметчика (кухня и др.): 1 поз. — в позиции «по КП» мебели и техники.

	Лист	№ док.	Подпись	Дата	Проект: Квартира 103 м²			
Дизайнер	Кырлан А.С.			14.11.26				
Проверил					Смета проекта: этапы, помещения, итог (окончание)	Стадия	Лист	Листов
Н. контр.								
Утв.						П	С8	129

выпуск 14.11.2026 № 32d0256903 · стр. 119 из 129

Смета материалов с ценами

№	Позиция	Ед.	Нетто	Запас	С запасом	К закупке (упаковка)	Цена за ед., ₽	Сумма, ₽	Заказать заранее	Доп.
Чистовая отделка — позиций 20, с ценой 11, итого 885 120 ₽										
Покрытия полов и облицовка										
1	Инженерная доска (дуб натуральный, рабочий слой 4 мм, эмиссия E1, прямая укладка) — 1167-4250	м²	82,52	7 %	88,30	88,30 м²	4 513 / м²	398 498		8
2	Керамогранит 600×600 мм Atlas Concorde Marvel Travertine Sand Cross 60×60 Matte Sensitech, арт. AFUL (той же коллекции, что стены A8UZ; тон сверить по образцу)	шт	23	13 %	26	26 шт · коробка	1 800 / м²	16 848		8
3	Керамогранит 600×1200 мм A8UZ	шт	86	14 %	98	98 шт · коробка	3 500 / м²	246 960		8
4	Керамогранит — керамогранит матовый, тон F497, 600×600×9 мм	м²	2,01	10 %	2,21	2,30 м²	1 800 / м²	4 140		1, 8
Лакокрасочные материалы										
5	Краска интерьерная акриловая, матовая, класс истирания 1 — Farrow & Ball Modern Emulsion No. 289 «Inchyra Blue — тёмный сине-серый»	л	8,54	10 %	9,39	4 банка · банка 2,5 л	5 800 / банк	23 200		8
6	Краска интерьерная акриловая, матовая, класс истирания 1 — Farrow & Ball Modern Emulsion No. 291 «School House White — тёплый меловой белый»	л	49,98	10 %	54,98	22 банка · банка 2,5 л	5 800 / банк	127 600		8
7	Краска интерьерная акриловая, глубокоматовая, класс истирания 2 — Tikkurila Anti-Reflex 2 S 0502-Y «Белый с лёгкой желтизной»	л	16,28	10 %	17,91	7 банка · банка 2,7 л	3 510 / банк	24 570		8
8	Краска интерьерная акриловая, матовая, класс истирания 1 — Tikkurila Harmony S 0502-Y «Белый с лёгкой желтизной»	л	7,08	10 %	7,79	3 банка · банка 2,7 л	3 510 / банк	10 530		8
9	Краска интерьерная акриловая, матовая, класс истирания 1 — Farrow & Ball Modern Emulsion No. 255 «Tanner's Brown — тёмный шоколад»	л	4,23	10 %	4,65	2 банка · банка 2,5 л	5 800 / банк	11 600		8
10	Краска интерьерная акриловая, матовая, класс истирания 1 — Tikkurila Luja 7 S 0502-Y «Белый с лёгкой желтизной»	л	1,45	10 %	1,59	1 банка · банка 2,7 л	3 510 / банк	3 510		8
Погонажные изделия и потолки										
11	Плинтус напольный МДФ под покраску, h=83 мм, крепление к стене — Ultrawood Base 5340, ЛДФ под окраску, 83×15 мм, 2440 мм (арт. LDF-BASE-5340)	м	103,48	10 %	113,83	48 шт · хлыст 2,4 м	368 / шт	17 664		8
Двери										
12	Дверь входная Д-1, проём 960×2100 мм	шт	1		1	1 шт	по запросу			6
13	Дверь скрытого монтажа (короб под покраску) Д-2, проём 800×2100 мм, UNION FILO-60 / INVISIBLE ФИЛО-60, ГРУНТ; ИНВИЗИБЛ | FILO-60, FONDO; INVISIBLE	шт	1		1	1 шт	по запросу		≈ 30 дн.	6, 7
14	Дверь скрытого монтажа (короб под покраску) Д-3, проём 700×2100 мм, UNION FILO-60 / INVISIBLE ФИЛО-60, ГРУНТ; ИНВИЗИБЛ | FILO-60, FONDO; INVISIBLE	шт	1		1	1 шт	по запросу		≈ 30 дн.	6, 7
15	Дверь скрытого монтажа (короб под покраску) Д-4, проём 800×2100 мм, UNION FILO-60 / INVISIBLE ФИЛО-60, ГРУНТ; ИНВИЗИБЛ | FILO-60, FONDO; INVISIBLE	шт	1		1	1 шт	по запросу		≈ 30 дн.	6, 7
16	Дверь скрытого монтажа (короб под покраску) Д-5, проём 700×2100 мм, UNION FILO-60 / INVISIBLE ФИЛО-60, ГРУНТ; ИНВИЗИБЛ | FILO-60, FONDO; INVISIBLE	шт	1		1	1 шт	по запросу		≈ 30 дн.	6, 7
17	Дверь скрытого монтажа (короб под покраску) Д-6, проём 700×2100 мм, UNION FILO-60 / INVISIBLE ФИЛО-60, ГРУНТ; ИНВИЗИБЛ | FILO-60, FONDO; INVISIBLE	шт	1		1	1 шт	по запросу		≈ 30 дн.	6, 7
18	Дверь скрытого монтажа (короб под покраску) Д-7, проём 700×2100 мм, UNION FILO-60 / INVISIBLE ФИЛО-60, ГРУНТ; ИНВИЗИБЛ | FILO-60, FONDO; INVISIBLE	шт	1		1	1 шт	по запросу		≈ 30 дн.	6, 7
19	Дверь скрытого монтажа (короб под покраску) Д-8, проём 800×2100 мм, UNION FILO-60 / INVISIBLE ФИЛО-60, ГРУНТ; ИНВИЗИБЛ | FILO-60, FONDO; INVISIBLE	шт	1		1	1 шт	по запросу		≈ 30 дн.	6, 7
20	Дверь скрытого монтажа (короб под покраску) Д-9, проём 700×2100 мм, UNION FILO-60 / INVISIBLE ФИЛО-60, ГРУНТ; ИНВИЗИБЛ | FILO-60, FONDO; INVISIBLE	шт	1		1	1 шт	по запросу		≈ 30 дн.	6, 7
Черновые материалы — позиций 12, с ценой 2, итого 25 400 ₽										
Покрытия полов и облицовка										
21	Клей для паркетной и инженерной доски (эластичный, по ТУ изготовителя доски)	м²	82,52		82,52	фасовка по ТУ изделия	по запросу			2
Сухие смеси и гидроизоляция										
22	Клей плиточный цементный класса C2 TE S1 (ГОСТ Р 56387-2018) — Ceresit CM 17 или аналог	кг	291,64	10 %	320,80	13 мешок · мешок 25 кг	1 800 / меш.	23 400		8
23	Затирка цементная класса CG2WA, цвет — по колерной карте — Mapei Ultracolor Plus 132 или аналог	кг	3,61	10 %	3,97	2 упаковка · упак. 2 кг	1 000 / упак.	2 000		8

	Лист	№ док.	Подпись	Дата
Дизайнер	Кырлан А.С.			14.11.26
Проверил				
Н. контр.				
Утв.				

Проект: Квартира 103 м²

Смета материалов с ценами	Стадия	Лист	Листов
	П	С9	129

Смета материалов с ценами (продолжение)

№	Позиция	Ед.	Нетто	Запас	С запасом	К закупке (упаковка)	Цена за ед., ₽	Сумма, ₽	Заказать заранее	Доп.
24	Гидроизоляция обмазочная полимерная, 2 слоя, лента в углах, манжеты на выводах	м²	17,01	10 %	18,71	фасовка по ТУ изделия	по запросу			2
25	Лента демпферная по периметру пола из плитки	м	24,68	10 %	27,15	28,00 м	по запросу			
26	Смесь цементно-песчаная для стяжки М200 (50 мм, 49 мм, 47 мм, 33 мм)	м³	4,95	5 %	5,20	фасовка по ТУ изделия	по запросу			2
27	Смесь штукатурная гипсовая для машинного и ручного нанесения по маякам, слой до 10 мм	м²	291,08	10 %	320,19	фасовка по ТУ изделия	по запросу			2
Короба из ГКЛВ										
28	Лист ГКЛВ 12,5 мм, 2500 × 1200 мм, обшивка коробов в 2 слоя	м²	6,46	10 %	7,11	3 лист · лист 3,00 м²	по запросу			
29	Профиль стальной оцинкованный 27 × 28 мм: каркас коробов (стойки и направляющие)	м	15,60	10 %	17,16	6 шт · хлыст 3 м	по запросу			
Лакокрасочные материалы										
30	Шпаклёвка финишная полимерная под окраску (стены и потолки, Q3)	м²	358,98	10 %	394,88	фасовка по ТУ изделия	по запросу			2
31	Грунтовка акриловая глубокого проникновения, 2 слоя	м²	391,80	10 %	430,98	фасовка по ТУ изделия	по запросу			2
Погонажные изделия и потолки										
32	Потолок подвесной ГКЛ/ГКЛВ по каркасу Knauf П113: листы, профили, подвесы, лента, шпаклёвка швов	м²	96,28		96,28	фасовка по ТУ изделия	по запросу			2
Электрика и слаботочные сети — позиций 41, с ценой 0, итого 0 ₽										
Слаботочные сети										
33	Кабель домофона — тип по системе поставщика	м	4,30		4,30	5,00 м	по запросу			3
34	Кабель коаксиальный RG-6 (75 Ом) к розеткам ТВ	м	16,10		16,10	17,00 м	по запросу			3
35	Кабель U/UTP кат. 6 (LAN, Wi-Fi и камеры по PoE)	м	70,30		70,30	71,00 м	по запросу			3
36	Гофротруба Ø20 для слаботочных линий, отдельно от силовых	м	81,60		81,60	82,00 м	по запросу			3
37	Розетка компьютерная RJ45, кат. 6, с рамкой и подрозетником	шт	4		4	4 шт	по запросу			
38	Розетка телевизионная (коаксиальная) с рамкой и подрозетником	шт	1		1	1 шт	по запросу			
39	Трубка или монитор домофона (поставка домофонной организации)	шт	1		1	1 шт	по запросу			
40	Щит слаботочный ЩС: корпус, DIN-рейка, розетки 220 В	шт	1		1	1 шт	по запросу			
41	Патч-панель, портов не менее 5	шт	1		1	1 шт	по запросу			
Электрика: силовая часть										
42	Кабель силовой ВВГнг(А)-LS 3×1,5 мм²	м	271,40		271,40	272,00 м	по запросу			3
43	Кабель силовой ВВГнг(А)-LS 3×2,5 мм²	м	308,30		308,30	309,00 м	по запросу			3
44	Кабель силовой ВВГнг(А)-LS 3×6 мм²	м	15,80		15,80	16,00 м	по запросу			3
Электрика: щит										
45	Автоматический выключатель C10 А, 1P	шт	4		4	4 шт	по запросу			4
46	Автоматический выключатель C16 А, 1P	шт	9		9	9 шт	по запросу			4
47	Автоматический выключатель C32 А, 1P	шт	1		1	1 шт	по запросу			4
48	Корпус щита ЩРВ-П-24, IP41, 24 модулей	шт	1		1	1 шт	по запросу			4
49	Вводной автомат C63, 2P	шт	1		1	1 шт	по запросу			4
50	Вводное УЗО-S 63 А, 100 мА (селективное)	шт	1		1	1 шт	по запросу			4
51	УЗИП тип 2	шт	1		1	1 шт	по запросу			4
Электрика: механизмы и изделия										
52	Розетка с з/к и защитными шторками, 16 А	шт	36		36	36 шт	по запросу			4
53	Розетка IP44 с крышкой, 16 А	шт	2		2	2 шт	по запросу			4

	Лист	№ док.	Подпись	Дата	Проект: Квартира 103 м²			
Дизайнер	Кырлан А.С.			14.11.26	Смета материалов с ценами (продолжение)	Стадия	Лист	Листов
Проверил						П	С10	129
Н. контр.								
Утв.								

Смета материалов с ценами (продолжение)

№	Позиция	Ед.	Нетто	Запас	С запасом	К закупке (упаковка)	Цена за ед., ₽	Сумма, ₽	Заказать заранее	Доп.
54	Выключатель 1-клав.	шт	2		2	2 шт	по запросу			4
55	Выключатель 1-клав. перекрёстный	шт	1		1	1 шт	по запросу			4
56	Выключатель 1-клав. проходной	шт	1		1	1 шт	по запросу			4
57	Выключатель 2-клав.	шт	5		5	5 шт	по запросу			4
58	Выключатель 2-клав. (перекрёстная + проходная)	шт	1		1	1 шт	по запросу			4
59	Выключатель 2-клав. (проходная + обычная)	шт	4		4	4 шт	по запросу			4
60	Выключатель 2-клав. проходной	шт	1		1	1 шт	по запросу			4
61	Светорегулятор 1-канальный, задний фронт (LED)	шт	1		1	1 шт	по запросу			4
62	Датчик движения ночной подсветки	шт	1		1	1 шт	по запросу			4
63	Рамка 1-постовая	шт	44		44	44 шт	по запросу			4
64	Рамка 2-постовая	шт	5		5	5 шт	по запросу			4
65	Коробка установочная (подрозетник) Ø68	шт	54		54	54 шт	по запросу			4
66	Вывод кабеля под прибор (клеммник)	шт	6		6	6 шт	по запросу			4
67	Коробка уравнивания потенциалов КУП	шт	2		2	2 шт	по запросу			4
68	Блок питания LED 24 В, 200 Вт, дим.	шт	3		3	3 шт	по запросу			4
69	Блок питания LED 24 В, 100 Вт, дим.	шт	1		1	1 шт	по запросу			4
70	Блок питания LED 24 В, 20 Вт	шт	1		1	1 шт	по запросу			4
71	Блок питания LED 24 В, 30 Вт	шт	1		1	1 шт	по запросу			4
72	Извещатель дымовой автономный	шт	4		4	4 шт	по запросу			4
73	Извещатель тепловой	шт	3		3	3 шт	по запросу			4
Сантехника — позиций 38, с ценой 0, итого 0 ₽										
Сантехника: санитарные приборы										
74	Ванна встраиваемая акриловая 1600×700 мм, с каркасом, экраном и отверстием слив-перелив	шт	1		1	1 шт	по запросу			5, 1
75	Унитаз подвесной безободковый, с сиденьем микролифт, крепёж и звукоизолирующая прокладка — Jacob Delafon Struktura EDF102-00	шт	2		2	2 шт	по запросу			5
76	Инсталляция для подвесного унитаза: рама высотой 1120 мм, бачок, клавиша смыва (ось клавиши 1050 мм от чистого пола)	шт	2		2	2 шт	по запросу			5, 1
77	Умывальник подвесной 600×450 мм, с отверстием под смеситель и переливом	шт	1		1	1 шт	по запросу			5, 1
78	Умывальник подвесной 500×450 мм, с отверстием под смеситель и переливом	шт	1		1	1 шт	по запросу			5, 1
79	Поддон душевой низкий 800×800 мм, с сифоном и выпуском Ø50, на ножках/подиуме	шт	1		1	1 шт	по запросу			5, 1
80	Мойка кухонная врезная / подстольная, с переливом, ориентир 700×480 мм — в модуле М-14 шириной 800 мм, вырез по шаблону модели	шт	1		1	1 шт	по запросу			5, 1
81	Полотенцесушитель электрический, IP44, с терморегулятором	шт	2		2	2 шт	по запросу			5, 1
Сантехника: смесители, сифоны и арматура приборов										
82	Смеситель для ванны настенный однорычажный, межосевое 150 мм, с душевым набором (лейка, шланг, держатель)	шт	1		1	1 шт	по запросу			5, 1
83	Смеситель для умывальника однорычажный, с донным клапаном	шт	2		2	2 шт	по запросу			5, 1
84	Душевая система скрытого монтажа с термостатом: встраиваемая часть, верхний душ, ручная лейка	шт	1		1	1 шт	по запросу			5, 1
85	Смеситель кухонный однорычажный, высокий излив	шт	1		1	1 шт	по запросу			5, 1
86	Обвязка ванны слив-перелив Ø40/50 с сифоном	шт	1		1	1 шт	по запросу			5, 1
87	Сифон для умывальника бутылочный Ø32/40–50, с гофрой к выпуску	шт	2		2	2 шт	по запросу			5, 1
88	Сифон для мойки Ø40/50	шт	1		1	1 шт	по запросу			5, 1

	Лист	№ док.	Подпись	Дата
Дизайнер	Кырлан А.С.			14.11.26
Проверил				
Н. контр.				
Утв.				

Проект: Квартира 103 м²

Смета материалов с ценами (продолжение)

Стадия	Лист	Листов
П	С11	129

Смета материалов с ценами (продолжение)

№	Позиция	Ед.	Нетто	Запас	С запасом	К закупке (упаковка)	Цена за ед., ₽	Сумма, ₽	Заказать заранее	Доп.
89	Сифон для посудомоечной машины с обратным клапаном, на выводе слива Ø40	шт	1		1	1 шт	по запросу			5, 1
90	Сифон для стиральной машины встраиваемый в стену Ø50, с обратным клапаном	шт	1		1	1 шт	по запросу			5, 1
91	Кран угловой ½"×½" с гибкой подводкой 40 см (умывальники, мойка)	шт	6		6	6 шт	по запросу			5, 1
92	Кран шаровой угловой ½"×¾" для подключения стиральной и посудомоечной машины	шт	2		2	2 шт	по запросу			5, 1
Сантехника: трубопроводы										
93	Труба полипропиленовая PP-R PN20 Ø20×3,4 (B1) — ГОСТ 32415-2013	м	19,00	10 %	19,00	19,00 м	по запросу			5
94	Труба PP-R, армированная стекловолокном, PN20 Ø20×2,8 (T3) — ГОСТ 32415-2013	м	12,00	10 %	12,00	12,00 м	по запросу			5
95	Труба канализационная ПП Ø40 (К1) — ГОСТ 32414-2013	м	1,00	10 %	1,00	1,00 м	по запросу			5
96	Труба канализационная ПП Ø50 (К1) — ГОСТ 32414-2013	м	8,50	10 %	8,50	8,50 м	по запросу			5
97	Труба канализационная ПП Ø110 (К1) — ГОСТ 32414-2013	м	4,50	10 %	4,50	4,50 м	по запросу			5
Сантехника: фасонные части и выводы										
98	Отвод канализационный ПП 45° Ø40 — ГОСТ 32414-2013	шт	2		2	2 шт	по запросу			5
99	Отвод канализационный ПП 45° Ø50 — ГОСТ 32414-2013	шт	24		24	24 шт	по запросу			5
100	Отвод канализационный ПП 45° Ø110 — ГОСТ 32414-2013	шт	12		12	12 шт	по запросу			5
101	Тройник канализационный ПП 45° (врезки ветвей) — ГОСТ 32414-2013	шт	8		8	8 шт	по запросу			5
102	Ревизия канализационная ПП (после поворота трассы) — ГОСТ 32414-2013	шт	11		11	11 шт	по запросу			5
103	Фитинги PP-R Ø20: тройники, угольники 90° (ветви и повороты B1, T3) — ГОСТ 32415-2013	шт	42		42	42 шт	по запросу			5
104	Водорозетка PP-R Ø20×½" настенная, с креплением — ГОСТ 32415-2013	шт	14		14	14 шт	по запросу			5
Сантехника: узлы ввода, люки, короба										
105	Кран шаровой латунный Ду15 PN16 (отключение ввода)	шт	8		8	8 шт	по запросу			5, 1
106	Фильтр сетчатый косой Ду15	шт	8		8	8 шт	по запросу			5, 1
107	Счётчик воды крыльчатый Ду15 (ХВ, ГВ), с поверкой	шт	8		8	8 шт	по запросу			5, 1
108	Клапан обратный Ду15	шт	8		8	8 шт	по запросу			5, 1
109	Люк ревизионный нажимной под плитку 300×400 мм	шт	4		4	4 шт	по запросу			5, 1
110	Звукоизоляция стояка К1 в коробе: рулонный звукоизоляционный материал ≥ 10 мм, обмотка стояка на высоту этажа	м	10,80		10,80	10,80 м	по запросу			5, 1
111	Короб К1 над полом: профиль ПН/ПС, ГКЛВ 12,5 мм под плитку	м	7,80		7,80	7,80 м	по запросу			5, 1
	ИТОГО материалы (позиций с ценой 13 из 111; без цены 98 — «по запросу», в итог не входят)							**910 520**		

Примечания

1. Количества — из единой книги материалов проекта: тот же расход, что в спецификации отделочных материалов, смете и списке покупок. Запас — на подрезку и бой; норма запаса печатается в графе «Запас», её основание — в отдельном документе «Смета на материалы».
2. Цены — нижняя граница открытых прайсов (прайсы собраны 21.09.2026, часть расценок сверена повторно 08.11.2026, Москва); не предложение (оферта) магазинов. Цены нет — «по запросу», позиция в итог не входит. Работы в эту смету не входят (они — на листе «Смета проекта»).
3. Доп. 1. Изделие не выбрано: позиция описана по характеристикам («аналог»); марка, артикул и цена определяются при выборе изделия.
4. Доп. 2. Фасовка не задана в данных: количество дано в мерах расчёта, число упаковок определяется по выбранному продукту (расход и тара — по ТУ).
5. Доп. 3. Длина кабеля — по длинам групп щита из данных электрика; запас на подрезку в длину не заложен — берите бухту с запасом 5–10 %.
6. Доп. 4. Механизмы, рамки и подрозетники — по ведомости изделий электрика; серию механизмов выбирает заказчик.
7. Доп. 5. Трубы и фасонные части — по трассам листа разводки, +10 % на подрезку (уже в количестве); модели приборов заказчик выбирает сам.
8. Доп. 6. Двери: цена и срок называет поставщик после выбора изделия; в смету стоят только если цена задана в данных.
9. Доп. 7. Срок поставки — из данных проекта; если срок не задан, указан типовой диапазон практики как ориентир, а не срок поставщика.
10. Доп. 8. Цена — нижняя граница открытых прайс-листов на дату сбора (книга цен проекта); не коммерческое предложение магазина.
11. Доп. 9. Доли по помещениям справочные: общая закупка делится пропорционально площади (длине, числу), по которой считается позиция.

	Лист	№ док.	Подпись	Дата
Дизайнер	Кырлан А.С.			14.11.26
Проверил				
Н. контр.				
Утв.				


Проект: Квартира 103 м²

Смета материалов с ценами (окончание)

Стадия	Лист	Листов
П	С12	129

1 Порог 15 мм: мокрая зона — смежное помещение (М 1:10)


Применение: двери Д-5, Д-9

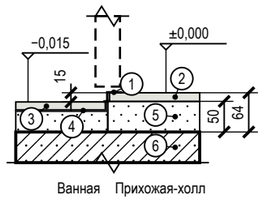

Поз.	Состав слоя, изделие
1	порог-переход металлический, перепад 15 мм, на клей-герметик
2	керамогранит на клею С2 TE S1
3	керамогранит на клею С2 TE S1
4	гидроизоляция в 2 слоя с подъёмом на торец ступени, лента в углу
5	ЦПС М200 50 мм; в мокрой зоне 33 мм
6	плита перекрытия

2 Дверь скрытого монтажа в плоскости стены, плинтус (М 1:5)


Применение: двери Д-2, Д-3, Д-4, Д-5, Д-6, Д-7, Д-8, Д-9

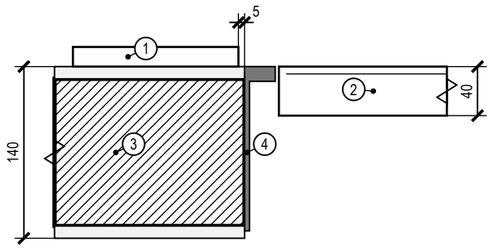

Поз.	Состав слоя, изделие
1	плинтус МДФ 83×16 на клей; у короба — зазор 5 мм, окраска в цвет стены
2	полотно 40 мм под окраску, заподлицо со стеной; теневой шов 3 мм
3	стена 120 мм, штукатурка 10 мм с двух сторон
4	короб скрытого монтажа (алюминий), лицом в плоскости отделки; монтаж до штукатурки

3 Короб стояков К1-1, К1-2 (кухня) с люком и звукоизоляцией (М 1:10)


Применение: пом. 6, 5, 11, 7

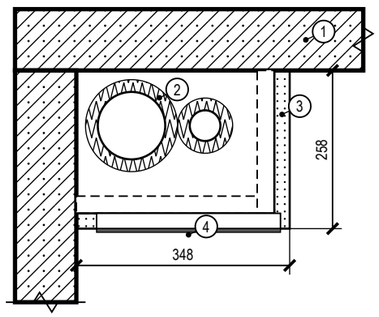

Поз.	Состав слоя, изделие
1	стены существующие — не ослаблять
2	звукоизоляция стояков рулонная 20 мм; К1-1 Ø110, К1-2 (кухня) Ø50
3	короб: профиль 27×28, ГКЛВ 2×12,5 мм, облицовка плиткой
4	ревизионный люк 300×400 мм нажимной, под плитку; против ревизии стояка

4 Гидроизоляция санузла: заход на стены 200 мм, примыкание ванны (М 1:20)


Применение: пом. 6, 11

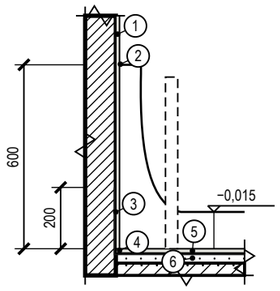

Поз.	Состав слоя, изделие
1	облицовка — плитка на клею С2 TE S1, затирка CG2WA
2	примыкание ванны: лента бордюрная + силиконовый санитарный герметик; облицовка опирается на борт
3	гидроизоляция обмазочная в 2 слоя, заход на стены 200 мм (в зоне душа — выше), до облицовки; акт скрытых работ, тест проливом
4	лента гидроизоляционная в углах и у трапов
5	керамогранит на клею С2 TE S1
6	ЦПС М200 33 мм

5 Плинтус МДФ 83×15 мм у окрашенной стены по доске (ламинату) (М 1:10)


Применение: пом. 1, 2, 3, 5, 7, 8, 9, 10

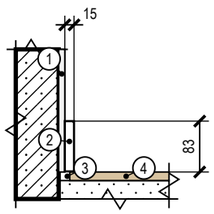

Поз.	Состав слоя, изделие
1	штукатурка, шпаклёвка Q3, окраска — по ведомости отделки
2	плинтус МДФ 83×15 под окраску в цвет стены; клей монтажный — к стене, не к полу
3	зазор покрытия у стены 8–10 мм закрывается плинтусом
4	инженерная доска дуб на клею

6 Плинтус МДФ 83×15 мм у окрашенной стены по керамограниту (плитке) (М 1:10)

Применение: пом. 4

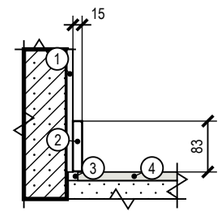

Поз.	Состав слоя, изделие
1	штукатурка, шпаклёвка Q3, окраска — по ведомости отделки
2	плинтус МДФ 83×15 под окраску в цвет стены; клей монтажный — к стене, не к полу
3	зазор покрытия у стены 8–10 мм закрывается плинтусом
4	керамогранит на клею С2 TE S1

Условные обозначения

- железобетон (плита, стены) — условно: конструкция не установлена
- кладка, перегородка — условно: конструкция не установлена
- стяжка, раствор
- гипсокартон ГКЛВ
- звукоизоляция, эластичный заполнитель
- плитка, керамогранит на клею
- инженерная доска (покрытие пола)
- металлический профиль (порог, Т-профиль, короб двери)
- гидроизоляция (обмазочная, лента)

Примечания

1. Узлы — типовые решения проекта для мест, отмеченных выносками на листе схемы расположения развёрток и узлов; размеры — в мм, отметки — в м от ±0,000.
2. Узлы с гидроизоляцией, закладными и коробами скрытого монтажа принимаются по актам скрытых работ до закрытия отделкой; гидроизоляция — после теста проливом (24 ч).
3. Марки изделий (порог, Т-профиль, короб скрытой двери, люк) — по спецификациям; замена — на аналог с теми же габаритами по согласованию с автором проекта.
4. Материал плиты перекрытия и стен в узлах показан условно (железобетон, кладка): конструкция дома не установлена — крепёж, анкеры и толщины слоёв уточняются после обследования (до него — по допущениям общих указаний).


	Лист	№ док.	Подпись	Дата
Дизайнер	Кырлан А.С.			14.11.26
Проверил				
Н. контр.				
Утв.				

Проект: Квартира 103 м²


Узлы	Стадия	Лист	Листов
	П	С13	129

выпуск 14.11.2026 № 32d0256903 · стр. 124 из 129

№	Работа	Нед.	После
Р-1	**демонтаж**	1,5	
Р-2	**контрольный обмер**	0,5	Р-1
Р-3	**черновая электрика**	2,25	Р-2
Р-4	черновая сантехника	1,5	Р-2
Р-5	**штукатурка**	3	Р-3, Р-4
Р-6	**стяжка**	1,25	Р-5
Р-7	**гидроизоляция**	0,75	Р-6
Р-8	ГКЛ	2,25	Р-3, Р-4
Р-9	**плитка**	4,25	Р-7, Р-8, Р-6
Р-10	**шпаклёвка**	3,5	Р-9, Р-8, Р-5
Р-11	**окраска**	2,75	Р-10
Р-12	**чистовые полы**	1,5	Р-11, Р-9
Р-13	**двери и плинтусы**	1,25	Р-12, Р-11
Р-14	**чистовая электрика и сантехника**	1,25	Р-13, Р-11
Р-15	**кухня и мебель**	1,5	Р-14, Р-13
Р-16	**сдача**	1	Р-15, Р-14

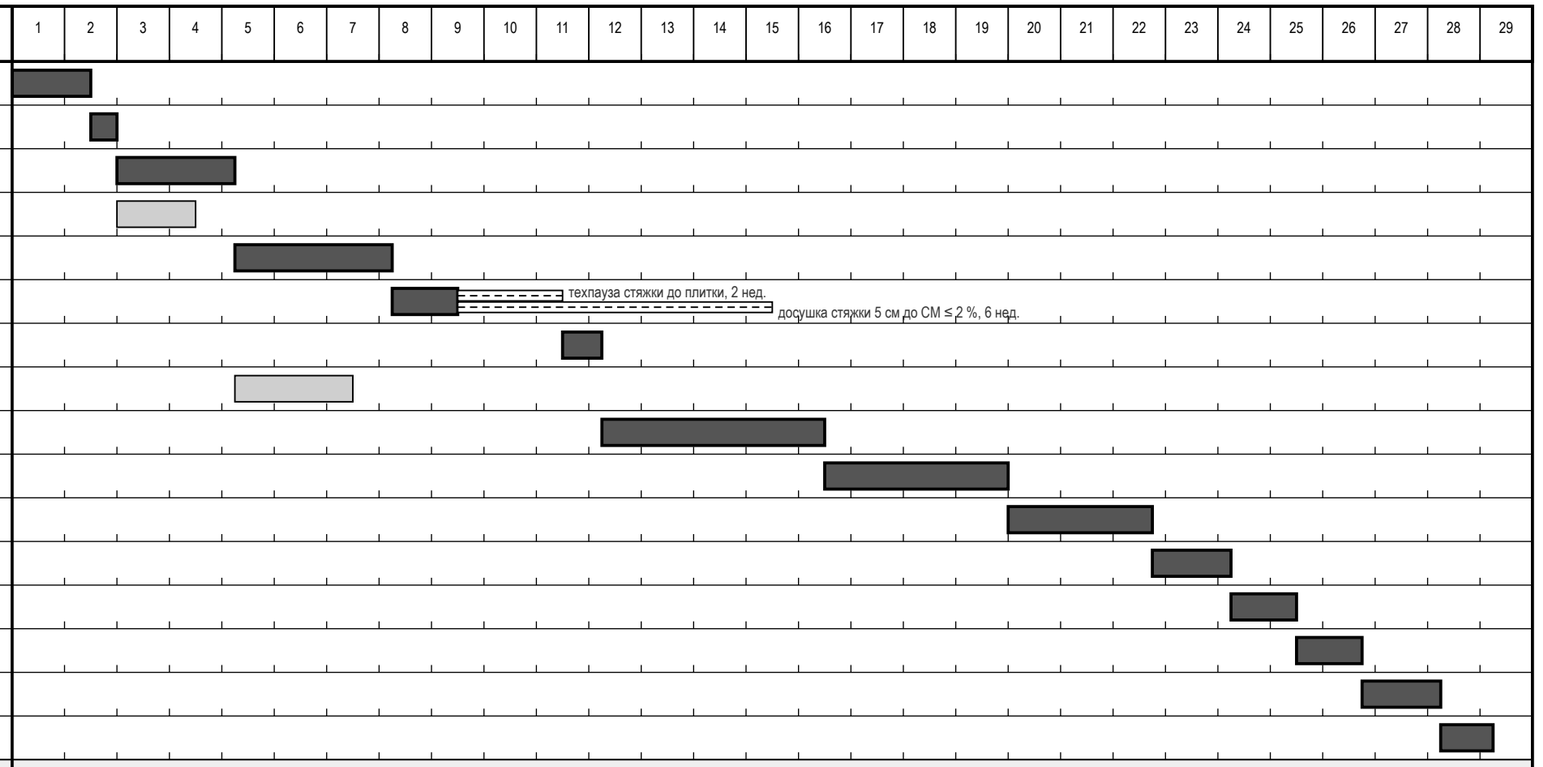

Закупки: заказать не позднее — «◆»; от заказа до поставки — штриховая полоса; срок поставки — только из данных или «ориентир практики»			
З-1	Двери скрытого монтажа с коробом под покраску в существующих проёмах: Д-2, Д-3, Д-4, Д-5,	4,25	для Р-5
З-2	Кухонный гарнитур по проекту кухни: модули М-14, М-15, М-16, М-17, М-18, М-19, М-21	6	для Р-15
З-3	Встраиваемая техника кухни: М-15 посудомоечная машина, М-17 духовой шкаф, М-19 холодильник, М-21 в		для Р-15
З-4	Стиральная машина: ОБ-02 (вертикальная загрузка 400 × 600 мм — условие закупки)		для Р-4
З-5	Сантехнические приборы и инсталляции: С-01, С-02, С-03, С-05, С-06, С-07		для Р-4
З-6	Керамогранит и плитка: 2 поз. по артикулу и формату, 51,07 м² по раскладке		для Р-9
З-7	Покрытие пола (доска) и плинтус: пом. 1, 2, 3, 5, 7, 8, 9, 10		для Р-12
З-8	Встроенная мебель по замеру цеха: М-11, М-24, М-29	6	для Р-15

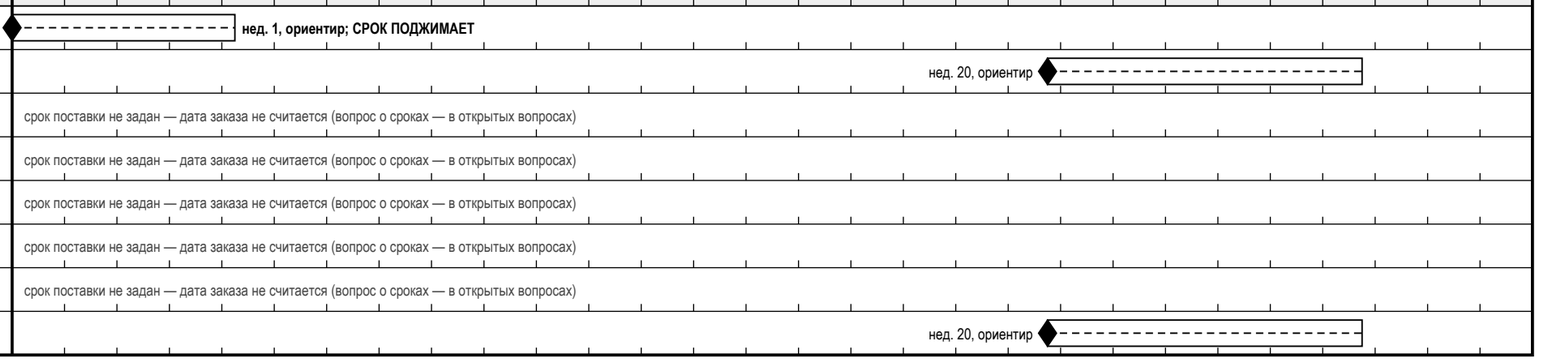

Итого: ≈ 28,25 нед. · жирная линия и тёмная полоса — критический путь

Примечания

1. Длительности этапов — типовые сроки по площади 100,72 м² (таблица «Свод для графика»: недели по этапам для 45, 80 и 120 м², середина вилки, линейная интерполяция); это ориентир, а не норма и не обещание бригады. Контрольный обмер — ориентир 0,5 нед. (в таблице нет).
2. Зависимости «после» — из графика закупок и работ (лист «График закупок и работ»); каждая работа начинается после конца предшественников. Техпаузы стоят отдельными полосами, а не спрятаны в длительности: стяжка → плитка — не менее 2 нед.; стяжка → чистовой пол — досушка стяжки 5 см до СМ ≤ 2 % — 6 нед. (ориентир «1 нед. на 1 см до 4 см, 5 см — 6 нед., 6 см — 8 нед.»; решает замер).
3. График последовательный и поэтому консервативный: в жизни шпаклёвка, плитка и досушка стяжки идут частично параллельно (таблица типовых сроков для 100,72 м²: 19–24 нед.). Совмещения — решение прораба после обмера.
4. Закупки: «заказать не позднее» = начало работы, которой нужна позиция, минус срок поставки. Срок поставки — из данных проекта (срок поставки позиции, срок изготовления обоев в отделке); если его нет, в графике стоит типовой диапазон практики с пометкой «ориентир» — это не срок поставщика, его надо получить до заказа. Кухню и встроенную мебель заказывают после замера по готовым стенам (после штукатурки). Позиции без срока дат заказа не имеют.
5. «Срок поджимает»: самая поздняя дата заказа раньше, чем позицию можно заказать (до замера или обмера): сдвиньте начало работ, ищите изделие с меньшим сроком или заказывайте по предварительному размеру — решение прораба и заказчика.

	Лист	№ док.	Подпись	Дата
Дизайнер	Кырлан А.С.			14.11.26
Проверил				
Н. контр.				
Утв.				

Проект: Квартира 103 м²

Календарный график работ и закупок	Стадия	Лист	Листов
	П	С14	129

выпуск 14.11.2026 № 32d0256903 · стр. 125 из 129

Приёмка по этапам: контрольные точки, допуски и акты скрытых работ

Этап	Контрольная точка (дальше не пускают без подписи)	Что проверяют	Чем	Допуск	Основание	Подпись	Акт скрытых работ / документ
Р-1	Демонтаж До начала демонтажа: запрошены документы на дом и БТИ	Что снимается и что не трогается: покрытия, отделка, дверные блоки; несущие стены и перегородки — без изменений	осмотр по плану демонтажа	снятое — только по плану; несущее не затрагивать	практика		Фото помещений до и после демонтажа; перечень снятого в журнале работ.
Р-2	Контрольный обмер Контрольный обмер на голых стенах сделан до заказа всего, что делают по размеру	Размеры помещений и проёмов, диагонали, положение стояков, щитка, каналов, толщины стен	рулетка, лазерный дальномер, уровень	допуск задаёт проект; расхождение с планом — в перечень открытых вопросов до заказа	практика		Протокол контрольного обмера с эскизом; расхождения занесены в открытые вопросы.
Р-3	Черновая электрика Черновая электрика: трассы, высоты подрозетников, замер изоляции подписаны до заделки	Сопротивление изоляции проводки (цепи до 1000 В)	мегаомметр	не менее 0,5 МОм	норматив (ПУЭ, гл. 1.8)		Акт скрытых работ на трассы проводки и слаботочные линии до закрытия штукатуркой и ГКЛ; исполнительная схема трасс с привязками; заземление и уравнивание потенциалов в санузле протокол и фото.
		Целостность и маркировка: PE жёлто-зелёный, N — синий, L — прочие цвета	визуально, прозвонка	каждый проводник промаркирован	практика		
		Высоты подрозетников и привязки — по плану розеток и выключателей	рулетка, уровень	по проекту; от чистого пола	практика		
Р-4	Черновая сантехника Черновая сантехника: опрессовка, отметки выводов, инсталляции подписаны до зашивки	Опрессовка водоснабжения: рабочее давление до 0,6 МПа — испытание 0,9 МПа; выше 0,6 МПа — по расчёту	опрессовочный насос, манометр	выдержка 10 мин (поквартирная); падение: пластик не более 0,06 МПа за 30 мин, сталь не более 0,05 МПа за 10 мин	практика (СП 73.13330)		Акт опрессовки (давление, время, результат); акт скрытых работ на трассы в стенах, полу и коробах; инсталляции, скрытые смесители, трапы — фото с рулеткой и отметками.
		Уклон канализации Ø40–50	уровень, построитель плоскостей	не менее 20 мм на 1 м	норматив (СП 30.13330)		
		Протечки в соединениях, сифоны, смесители, гибкая подводка	осмотр под давлением, салфетка на стыках	нет капель и влажных следов в контрольное время	практика		
		Отметки выводов и положение инсталляций до зашивки и гидроизоляции	рулетка в кадре, фото	по листу выводов	практика		
Р-5	Штукатурка Маяки стен проверены до штукатурки; коробки скрытых дверей стоят до штукатурки	Отклонение от вертикали (простая / улучшенная / высококачественная штукатурка)	отвес, лазерный уровень	3 / 2 / 1 мм на 1 м; не более 15 / 10 / 5 мм на высоту	практика (СП 71.13330.2017)		Фото коробок скрытых дверей с отметкой чистого пола — до штукатурки; класс штукатурки (простая / улучшенная / высококачественная) назван в договоре.
		Отклонение от горизонтали	уровень, правило	3 / 2 / 1 мм на 1 м; не более 15 / 10 / 5 мм на длину	практика (СП 71.13330.2017)		
		Неровности (плоскостность)	правило 2 м и щуп	до 5 / 3 / 2 мм на 1 м; не более 3 / 2 / 2 неровностей на 4 м²	практика (СП 71.13330.2017)		
		Влажность основания перед шпаклёвкой и отделкой	влагомер	верхние 20–30 мм — не более 5 % по массе	норматив (СП 71, табл. 7.2)		
Р-6	Стяжка Стяжка: подготовка, после заливки ровность, затем замер СМ перед чистовым полом	Ровность: просвет под рейкой 2 м	рейка 2 м, клиновой щуп	под паркет, ламинат — 2 мм; под гидроизоляцию до 4 мм; прочие покрытия — до 6 мм (цифры расходятся между источниками — сверить перед актом)	практика (СП 29.13330)		Акт скрытых работ на стяжку (толщина, армирование) до чистового пола; протокол ровности и протокол СМ-влажности; звукоизоляция и демпферная лента под стяжкой — фото и паспорт; контуры тёплого пола до заливки — схема укладки и замер сопротивления.
		Отклонение от горизонтали по помещению	уровень, нивелир	не более 0,2 % длины помещения	практика (СП 29.13330)		

	Лист	№ док.	Подпись	Дата	Проект: Квартира 103 м²			
Дизайнер	Кырлан А.С.			14.11.26	Чек-лист приёмки по этапам. Лист 1 из 3	Стадия	Лист	Листов
Проверил						П	С15	129
Н. контр.								
Утв.								

Приёмка по этапам: контрольные точки, допуски и акты скрытых работ (продолжение)

Этап	Контрольная точка (дальше не пускают без подписи)	Что проверяют	Чем	Допуск	Основание	Подпись	Акт скрытых работ / документ
		Число точек измерения	рейка	не менее 3 на 30 м² или 1 на небольшое помещение	практика		
		Отслоения и пустоты	простукивание молотком или киянкой	глухой звук — зона вскрывается и переделывается	практика		
		Влажность перед укладкой доски: цементная стяжка	влагомер; СМ-замер	ЦПС не более 2,0 % СМ (с тёплым полом не более 1,8 %); влагомер для плитки — не более 5 %	практика (СП 71; рекомендации производителей)		
Р-7	Гидроизоляция Гидроизоляция: пролив 24 ч подпись до плитки	Заведение на стены не ниже 200 мм от чистого пола; за ванной — 300 мм выше борта; в душе без поддона — на высоту лейки	рулетка	не менее 200 мм	норматив (СП 71.13330.2017, п. 8.6.5); остальное — практика		Акт теста проливом, фото узлов и высоты заведения на стены — до плитки.
		Тест проливом: слой воды 10–30 мм, контроль уровня и потолка соседа снизу	линейка, визуально	24 ч (минимум 12 ч); падения уровня и протечки нет	практика		
		Два слоя обмазки с межслойной сушкой, лента в углах и манжеты на выводах	визуально	по инструкции производителя	практика		
Р-8	ГКЛ Короба, ниши и потолки: черновые сети в зоне коробов приняты до обшивки	Шаг саморезов, отступ от кромки, заделка стыков (как у перегородок)	рулетка, визуально	потолок 150 мм; кромка 5–10 мм; стык — лента и 2 слоя шпаклёвки	практика (СП 163.1325800.2014)		Акт скрытых работ: каркас ГКЛ, закладные, звукоизоляция — фото до обшивки; воздуховоды в коробах и за потолком — фото и схема.
		Закладные под тяжёлое, карнизы, подвесные светильники на месте до обшивки	фото с привязками	по плану потолков и узлам	практика		
		Ревизионные люки: доступ к арматуре и ревизиям сохранён	осмотр	по листу ВК	практика		
Р-9	Плитка Раскладка плитки: первая плита и первый ряд проверены по развёртке; плитка выбрана, калибр партии измерен	Уступы между смежными плитками	линейка, на просвет	не более 1 мм	норматив (СП 71.13330.2017)		Раскладка подписана до начала плитки; протокол первого ряда; акт теста проливом приложен (этап гидроизоляции).
		Ширина шва и его прямолинейность	линейка, калибр	до 6 мм ручная укладка; фактическая по проекту ±0,5 мм	практика		
		Отклонение рядов от вертикали и горизонтали	уровень, правило, отвес	1,5 мм на 1 м длины	практика		
		Ровность облицовки	правило 2 м и щуп	не более 2–4 мм (цифра расходится по источникам)	практика		
		Пустоты под плиткой	простукивание всей площади	до 10 % площади допустимо; свыше 25 % под одной плиткой — брак	практика		
Р-10	Шпаклёвка Шпаклёвка Q3/Q4: проверка боковым светом до окраски	Класс основания под окраску: Q3 — сплошное финишное шпаклевание; Q4 — под направленный свет	переносной прожектор у поверхности под острым углом	Q3: царапины от абразива до 0,5 мм; Q4 — без видимых царапин и теней; неровность на 2 м: Q3 — 1 мм, Q4 — 0,5 мм	практика (Q-классы — не норматив СП, а согласованный критерий)		Класс (Q3 или Q4) назван в договоре; грунтование и армирование стыков перед шпаклёвкой — запись в журнале.
Р-11	Окраска Выкрасы утверждены, колеровка одной партией	Окраска без полос, подтёков, пропусков; цвет — по колерной карте	боковой свет, образец выкраса	без видимых дефектов при боковом свете	практика		Утверждённые выкрасы; остаток колеровки одной партии — для подкраски.
		Основание сухое, огрунтованное; защита от прямого солнца при высыхании	осмотр	по ТУ краски	норматив (СП 71.13330.2017, п. 7.5.2)		

	Лист	№ док.	Подпись	Дата
Дизайнер	Кырлан А.С.			14.11.26
Проверил				
Н. контр.				
Утв.				

Проект: Квартира 103 м²

Чек-лист приёмки по этапам. Лист 2 из 3

Стадия	Лист	Листов
П	С16	129

Приёмка по этапам: контрольные точки, допуски и акты скрытых работ (продолжение)

Этап	Контрольная точка (дальше не пускают без подписи)	Что проверяют	Чем	Допуск	Основание	Подпись	Акт скрытых работ / документ
Р-12	Чистовые полы Чистовые полы: влажность, ровность, уступы, зазоры — до укладки доски; мокрые работы закончены	Деформационный зазор у стен и порогов (доска, ламинат)	линейка, клинья при укладке	8–15 мм (чаще 10 мм); у ламината 5–10 мм по СП 71	практика (требования производителей); норматив (СП 71, п. 8.10.14)		Протокол СМ-влажности стяжки до укладки; паспорт и партия доски.
		Перепад основания под покрытие	правило 2 м и щуп	не более 2 мм на 2 м	практика		
		Зазоры и перепады между досками; скрип; видимый зазор в замке — брак	щуп, рука, шаг	«ступеньки» нет	практика		
		Влажность помещения при укладке и после	гигрометр	не более 60 %, без сквозняков	норматив (СП 71, п. 8.1.7)		
Р-13	Двери и плинтусы Полотна и плинтусы — после чистового пола; скрытые полотна после чистовой отделки стен	Отклонение коробки от вертикали	отвес, уровень	1,5 мм на 1 м, не более 3 мм на коробку	практика (ТР 105-00, пересказ)		Коробки скрытых дверей приняты до штукатурки (этап штукатурки); паспорт на полотна.
		Зазор между полотном и коробкой по периметру	щуп	2–4 мм по бокам и верху (единого норматива нет)	практика		
		Открывание и закрывание: без перекоса, плавный ход петель и доводчика	визуально, от руки	без задевания коробки и пола	практика		
Р-14	Чистовая электрика и сантехника Чистовая электрика и сантехника: протокол электролаборатории и проверка УЗО до подписи акта	УЗО: кнопка «Тест»; время отключения; ток отключения	кнопка на аппарате; прибор проверки УЗО (не мультиметр)	отключает; не более 0,3 с; 50–100 % от IΔn	практика измерений		Протокол измерений аккредитованной электролаборатории (изоляция по группам, УЗО, РЕ, фаза-ноль); исполнительная схема щита; акт опрессовки приложен (этап ВК).
		Сопротивление изоляции готовых линий; петля фаза-ноль для срабатывания автоматов	мегаомметр; прибор петли фаза-ноль	изоляция не менее 0,5 МОм; петля — по проекту	норматив (ПУЭ, гл. 1.8) / по проекту		
		Смесители, сифоны, гибкая подводка: пробный пуск воды	визуально под нагрузкой	нет подтёков в контрольное время	практика		
Р-15	Кухня и мебель Кухня и мебель: замер кухни снят по готовым стенам; чистовая электрика и сантехника подведены	Привязка выводов и розеток к модулям кухни; вытяжка, вентиляция	рулетка, сверка с листом кухни	по проекту кухни	практика		Акт передачи кухни; паспорта техники и гарантийные талоны.
		Тяга вентиляции у решёток	лист бумаги у решётки	бумага притягивается; при сомнениях — замер анемометром	практика		
Р-16	Сдача Финальная приёмка по таблицам СП 71: дефектная ведомость и акт	Стены, потолки, полы, плитка, двери, окна осмотр по чек-листу этапов выше	правило 2 м, уровень, щуп, боковой свет, влагомер	по таблицам выше	практика		Дефектная ведомость и акт приёмки; гарантия: по умолчанию претензии по качеству работ — 2 года, в договоре прописывается отдельно.
		Полный пакет документов: акты скрытых работ, протокол электролаборатории, акт опрессовки, исполнительные схемы, гарантийные обязательства	комплектность	пакет собран до подписи акта	практика		

Примечания

1. Метка основания: «норматив» — цифра подтверждена текстом СП, ГОСТ или ПУЭ; «практика» — отраслевая конвенция или один источник: к спору не годится без сверки первоисточника (СП 71.13330.2017, СП 29.13330, СП 163.1325800.2014, ПУЭ гл. 1.8, СП 73.13330, СП 30.13330).
2. Класс штукатурки (простая / улучшенная / высококачественная) и класс основания под окраску (Q3 или Q4) называются в договоре подряда: допуск выбирается по ним. Q-классы — не норматив, а согласованный сторонами критерий.
3. Акт скрытых работ подписывают до того, как работа закрыта следующим слоем (штукатуркой, плиткой, стяжкой, обшивкой): постфактум он слабее — осматривать нечего. Подписывают заказчик (или технадзор), подрядчик; при перепланировке — автор проекта. Каждую зону снимают до закрытия с рулеткой в кадре и привязкой к стене.
4. По умолчанию, если срок не прописан в договоре, претензии по качеству работ можно предъявить в течение 2 лет со дня приёмки; в договоре гарантийный срок и сроки на скрытые работы рекомендуется назвать явно.

	Лист	№ док.	Подпись	Дата	Проект: Квартира 103 м²			
Дизайнер	Кырлан А.С.			14.11.26	Чек-лист приёмки по этапам. Лист 3 из 3	Стадия	Лист	Листов
Проверил						П	С17	129
Н. контр.								
Утв.								

выпуск 14.11.2026 № 32d0256903 · стр. 128 из 129

Какому мастеру какие листы (номера — как в штампе)

Мастер	Что делает по альбому	Листы	Кроме чертежей — документы	Листов
Замерщик и прораб (до начала работ)	Контрольный обмер на голых стенах, сверка размеров и диагоналей, ответы на открытые вопросы до заказа	22–23, 25, 103–104	Задание на контрольный обмер; лист открытых вопросов	5
Гипсокартонщик и монтажник перегородок	Демонтаж и возведение перегородок, каркас, короба инсталляции, ниши, потолки; закладные под навесное	26–29, 52–55	Ведомость материалов каркаса; акт скрытых работ на каркас	8
Электрик	Группы щита, подрозетники и высоты, трассы, свет, управление светом, слаботочка, тёплый пол	56–63, 69–102	Таблица нагрузок; ведомость изделий; протокол электролаборатории	42
Сантехник	Выводы воды и канализации, разводка, аксонометрии, инсталляции, короба стояков	38–47, 69–102	Спецификация ВК; акт опрессовки; акт пролива	44
Монтажник вентиляции, отопления и кондиционеров	Вентиляция, радиаторы и тёплые полы, кондиционеры: места, размеры, трассы и дренаж	64–65	Акт опрессовки азотом (кондиционеры); фото воздуховодов до закрытия	2
Штукатур, шпаклёвщик, маляр, паркетчик	Основание стен, окраска и обои по колерной карте, полы и пороги, плинтус, узлы стыков	30–32, 66, 69–102, С1–С3, С13	Колерная карта и выкрасы; спецификация отделочных материалов	42
Плиточник	Раскладка и подрезка плитки стен, пола и фартука, гидроизоляция, швы, выводы в плитке	43–46, 48–49, 67–102, С13	Ведомость плитки; акт теста проливом	43
Монтажник дверей и окон	Заполнение проёмов: размеры коробок, открывание, пороги, скрытые двери	50–51	Ведомость проёмов; паспорта на полотна	2
Мебельщик, кухонный монтажник	Кухня и мебель на заказ: габариты, членение, фурнитура, связка с электрикой и сантехникой	27–29, 33–37, Д1–Д7	Ведомость изделий; замер кухни по готовым стенам	15
Заказчик и комплектатор	Что и когда покупать, сколько с запасом, во что это обойдётся; свет, декор и текстиль; визуализации как должно получиться	1–21, 24, 62, С4–С12, С14	Список покупок; смета; календарный график	33
Прораб и технадзор (приёмка)	Приёмка этапов, акты скрытых работ, дефектная ведомость	С14–С18	Чек-лист приёмки по этапам; календарный график	5

Примечания

1. Номера листов — как в основной надписи: основные подряд (1, 2, 3…), «Д» — детализация мебели, «С» — ведомости, спецификации, узлы и сметы, «П» — приложение единого комплекта. «12–18» — все листы с 12 по 18.
2. Лист может быть у нескольких мастеров: развёртка стены нужна электрику (высоты точек), сантехнику (выводы), отделочнику (материалы) и плиточнику (раскладка). Общие листы (обмер, список листов, перечень вопросов) прораб раздаёт всем.
3. Мастер работает по чертежам и берёт в руки то, что назначено ему здесь; закупки, смету и график ведёт заказчик с прорабом. Лист, которого нет в таблице ни у одного мастера, — вопрос прорабу: чей он.

	Лист	№ док.	Подпись	Дата	Проект: Квартира 103 м²			
Дизайнер	Кырлан А.С.			14.11.26				
Проверил					Лист → мастер	Стадия	Лист	Листов
Н. контр.								
Утв.						П	С18	129