LINEA

РАБОЧАЯ ДОКУМЕНТАЦИЯ

Дом 120 м²

Шифр комплекта ГД-2026-012-АИ

Стадия РП

Дата выпуска 19.10.2026

ПРЕДВАРИТЕЛЬНО · не для производства работ
открыто пунктов: 6 (реестр — л. 6)

ДИЗАЙНЕР

Кырлан Александр Сергеевич

выпуск 19.10.2026 · 53e4f7ddae · стр. 1 из 160

Содержание

ПРЕДВАРИТЕЛЬНО · не для производства работ · открыто пунктов: 6 (реестр — л. 6)

03 Общие данные 23 л.

26 Планировочное решение 10 л.

37 Электрооборудование 36 л.

74 Декор и текстиль 22 л.

97 Развёртки и узлы 32 л.

130 Смета 7 л.

138 Визуализации 22 л.

выпуск 19.10.2026 · 53e4f7ddae · стр. 2 из 160

ДИЗАЙН-ПРОЕКТ ИНТЕРЬЕРА

Дом 120 м²

Средиземноморский

147,36 м²

солнце и воздух · морская свежесть · неторопливость · тёплая простота · жизнь на террасе

Средиземноморский 60 % + скандинавский (scandinavian.json) 40 %: дом у соснового бора, светлый и солнечный. Стены — кремовый белый Calla G503 и известковый Wimborne White No. 239, потолки — Loft White No. 222; второй план светлый песок S 1010-Y20R, морская лазурь Lulworth Blue No. 89, серо-оливковая листва Treron No. 292; акценты эгейский синий S 3050-R80B, охра India Yellow No. 66, олива S 5020-G90Y. По брифу: дерево — дуб табак (мебель, лестница), фурнитура и светильники — латунь, рамы и металл — тёплый графит; свет тёплый 2700–3000 K, фасады матовые.

ПАЛИТРА 60 / 30 / 10

G503	F&B No. 239	Little Greene No. 222	NCS S 1010-Y20R	F&B No. 89
60 %	60 %	60 %	30 %	30 %

Визуализация 1 · Вид сверху (3D): планировка с мебелью, текстилем и декором

ОБЪЕКТ	ОБЩАЯ ПЛОЩАДЬ	ПОМЕЩЕНИЙ
Дом 120 м²	147,36 м²	13, из них жилых 5
СТИЛЬ	**СТАДИЯ**	**ШИФР**
Средиземноморский	Рабочий проект · предварительно	ГД-2026-012-АИ

АВТОР ПРОЕКТА

Кырлан Александр Сергеевич

Октябрь 2026

Изм.	Кол.уч	Лист	№ док.	Подп.	Дата
Разраб.		Кырлан А.С.			19.10.26
Пров.					
ГИП					
Н. контр.					
Утв.					

ГД-2026-012-АИ

Дом 120 м²

Общая площадь 147,36* м² · * размеры приняты, не замерены (реестр — л. 6, К-1)

Дизайн-проект интерьера	Стадия	Лист	Листов
	РП	1	130

Титульный лист

М б/м

Кырлан Александр Сергеевич

выпуск 19.10.2026 № 53e4f7ddae · стр. 3 из 160

Общие данные

Комплект ГД-2026-012-АИ · Дом 120 м² в два этажа (демо LINEA)

ПРЕДВАРИТЕЛЬНО · не для производства работ · открыто пунктов: 6 (реестр — л. 6)

Допущения и предложения на листе. Знак «*» принято (замерить). См. лист открытых вопросов (лист 6).

Ведомость рабочих чертежей основного комплекта ГД-2026-012-АИ

Лист	Наименование	Примечание
1	Титульный лист	
2	Общие данные	
3	Общие данные	
4	Общие данные	
5	Общие данные	
6	Открытые вопросы, принятые допущения и конфликты	
7	Задание на контрольный обмер и обследование. Лист 1 из 3	
8	Задание на контрольный обмер и обследование. Лист 2 из 3	
9	Задание на контрольный обмер и обследование. Лист 3 из 3	
10	График закупок и работ. Лист 1 из 3	
11	График закупок и работ. Лист 2 из 3	
12	График закупок и работ. Лист 3 из 3	
13	Обмерный план · 1-й этаж	
14	Обмерный план · 2-й этаж	
15	План демонтажа и монтажа перегородок · 1-й этаж	
16	План демонтажа и монтажа перегородок · 2-й этаж	
17	План дверей и ведомость заполнения проёмов · 1-й этаж	
18	План дверей и ведомость заполнения проёмов · 2-й этаж	
19	Лестница Л-1*	
20	Концепция интерьера · 1-й этаж	
21	Концепция интерьера · 2-й этаж	
22	План расстановки мебели · 1-й этаж	
23	План расстановки мебели · 2-й этаж	
24	Спецификация мебели и оборудования	
25	Спецификация мебели и оборудования (продолжение)	
26	Спецификация мебели и оборудования (продолжение)	
27	Спецификация мебели и оборудования (продолжение)	
28	План розеток и электровыводов · 1-й этаж	
29	План розеток и электровыводов · 2-й этаж	
30	План освещения · 1-й этаж	

Ведомость рабочих чертежей основного комплекта ГД-2026-012-АИ (продолжение)

Лист	Наименование	Примечание
31	План освещения · 2-й этаж	
32	План выключателей и схема включения · 1-й этаж	
33	План выключателей и схема включения · 2-й этаж	
34	Ведомость электроточек и изделий	
35	Ведомость электроточек и изделий (продолжение)	
36	Однолинейная схема щита	
37	Однолинейная схема щита (продолжение)	
38	План принципиальных трасс · 1-й этаж	
39	План принципиальных трасс · 2-й этаж	
40	План слаботочных сетей · 1-й этаж	
41	План слаботочных сетей · 2-й этаж	
42	План вентиляции · 1-й этаж	
43	План вентиляции · 2-й этаж	
44	План отопления · 1-й этаж	
45	План отопления · 2-й этаж	
46	План выводов сантехники · 1-й этаж	
47	План выводов сантехники · 2-й этаж	
48	Схема разводки водопровода и канализации · 1-й этаж	
49	Схема разводки водопровода и канализации · 2-й этаж	
50	Спецификация сантехнического оборудования	
51	Спецификация светильников и сценарии освещения	
52	План потолков · 1-й этаж	
53	План потолков · 2-й этаж	

Общие указания — лист 5: ±0,000 — чистый пол; несущие конструкции и сети дома — по отдельному проекту; скрытые работы — по актам. Открытые вопросы и допущения — лист 6.

Изм.	Кол.уч	Лист	№ док.	Подп.	Дата
Разраб.		Кырлан А.С.			19.10.26
Пров.					
ГИП					
Н. контр.					
Утв.					

ГД-2026-012-АИ

Дом 120 м²

Общая площадь 147,36* м² · * размеры приняты, не замерены (реестр — л. 6, К-1)

Дизайн-проект интерьера

Стадия	Лист	Листов
РП	2	130

Общие данные

М б/м

Кырлан Александр Сергеевич

выпуск 19.10.2026 № 53e4f7ddae · стр. 4 из 160

Общие данные

Комплект ГД-2026-012-АИ · лист 2 общих данных (продолжение)

Ведомость рабочих чертежей основного комплекта ГД-2026-012-АИ (продолжение)

Лист	Наименование	Примечание
54	Раскладка плитки. Планы полов	
55	Раскладка плитки. Прихожая. Фартук кухни	
56	Раскладка плитки. Санузел гостевой. Развёртки стен	
57	Раскладка плитки. Санузел второго этажа. Развёртки стен	
58	План полов · 1-й этаж	
59	План полов · 2-й этаж	
60	Ведомость отделки помещений. Лист 1 из 2	
61	Ведомость отделки помещений. Лист 2 из 2	
62	Колерная карта · 1-й этаж	
63	Колерная карта · 2-й этаж	
64	Колерная карта	
65	Спецификация отделочных материалов	
66	Спецификация отделочных материалов	
67	Концепция декора и визуализации	
68	План текстиля и декора · 1-й этаж	
69	План текстиля и декора · 2-й этаж	
70	Шторы и карнизы	
71	Ведомость текстиля	
72	Ведомость текстиля (продолжение)	
73	Ведомость декора. Схемы развески	
74	Встроенная мебель. Схема расположения · 1-й этаж	
75	Встроенная мебель. Схема расположения · 2-й этаж	
76	Шкаф-купе Пр1	
77	Шкаф распашной М4	
78	Шкаф распашной Д3	
79	Система хранения Гд1	
80	Система хранения Гд2	
81	Система хранения Кл1	
82	Система хранения Кл2	
83	Шкаф распашной Д8 Допущения и предложения на листе. См. лист открытых вопросов (лист 6).	

Ведомость рабочих чертежей основного комплекта ГД-2026-012-АИ (продолжение)

Лист	Наименование	Примечание
84	Система хранения Д10	
85	Кухня (пом. 1). Развёртка гарнитура	
86	Кухня (пом. 1). Монтажная схема	
87	Кухня (пом. 1). Развёртка гарнитура	
88	Кухня (пом. 1). Монтажная схема	
89	Шкафы. Монтажная схема. Лист 1 из 2	
90	Шкафы. Монтажная схема. Лист 2 из 2	
91	Ведомости изделий, техники и фурнитуры	
92	Реестр марок отделки и позиций альбома	
93	Реестр марок отделки и позиций альбома (продолжение)	
94	Схема расположения развёрток и узлов	
95	Развёртка стены А. Гостиная-кухня (пом. 1), кухонный фронт	
96	Развёртка стены Б. Гостиная-кухня (пом. 1), кухонный фронт	
97	Развёртка стены В. Гостиная-кухня (пом. 1)	
98	Развёртка стены Г. Гостиная-кухня (пом. 1)	
99	Развёртки стен А, В. Холл с лестницей (пом. 2)	
100	Развёртка стены Г. Холл с лестницей (пом. 2)	
101	Развёртки стен А, Б. Кабинет (пом. 3)	
102	Развёртки стен В, Г. Кабинет (пом. 3)	
103	Развёртки стен А, Б. Санузел гостевой (пом. 4)	
104	Развёртки стен В, Г. Санузел гостевой (пом. 4)	
105	Развёртки стен А1, А2, Б. Прихожая (пом. 5)	
106	Развёртки стен В, Г1, Г2. Прихожая (пом. 5)	

Общие указания — лист 5: ±0,000 — чистый пол; несущие конструкции и сети дома — по отдельному проекту; скрытые работы — по актам. Открытые вопросы и допущения — лист 6.

Изм.	Кол.уч	Лист	№ док.	Подп.	Дата
Разраб.		Кырлан А.С.			19.10.26
Пров.					
ГИП					
Н. контр.					
Утв.					

ГД-2026-012-АИ

Дом 120 м²

Общая площадь 147,36* м² · * размеры приняты, не замерены (реестр — л. 6, К-1)

Дизайн-проект интерьера

Стадия	Лист	Листов
РП	3	130

Общие данные

М б/м

Кырлан Александр Сергеевич

выпуск 19.10.2026 № 53e4f7ddae · стр. 5 из 160

Общие данные

Комплект ГД-2026-012-АИ · лист 3 общих данных (продолжение)

Ведомость рабочих чертежей основного комплекта ГД-2026-012-АИ (продолжение)

Лист	Наименование	Примечание
107	Развёртки стен А, Б. Спальня родителей (пом. 6)	
108	Развёртки стен В, Г. Спальня родителей (пом. 6)	
109	Развёртки стен А, Б. Детская (пом. 7)	
110	Развёртки стен В, Г. Детская (пом. 7)	
111	Развёртки стен А, Б, В. Гардеробная (пом. 8)	
112	Развёртка стены Г. Гардеробная (пом. 8)	
113	Развёртки стен. Кладовая (пом. 9)	
114	Развёртки стен А, В. Холл второго этажа (пом. 10)	
115	Развёртка стены Г. Холл второго этажа (пом. 10)	
116	Развёртки стен. Коридор второго этажа (пом. 11)	
117	Развёртки стен А, Б. Детская вторая (пом. 12)	
118	Развёртки стен В, Г. Детская вторая (пом. 12)	
119	Развёртка стены А. Санузел второго этажа (пом. 13)	
120	Развёртка стены Б. Санузел второго этажа (пом. 13)	
121	Развёртка стены В. Санузел второго этажа (пом. 13)	
122	Развёртка стены Г. Санузел второго этажа (пом. 13)	
123	Узлы	
124	Ведомость объёмов работ	
125	Ведомость объёмов работ (продолжение)	
126	Ведомость объёмов работ (окончание)	
127	Спецификация материалов	
128	Спецификация материалов (окончание)	
129	Смета ориентировочная	
130	Смета ориентировочная (окончание)	

Ведомость ссылочных и прилагаемых документов

Обозначение	Наименование	Примечание
	Ссылочные документы	
ГОСТ 21.201-2011	СПДС. Условные графические изображения элементов зданий, сооружений и конструкций	
ГОСТ 21.205-2016	СПДС. Условные обозначения элементов санитарно-технических систем	
ГОСТ 21.210-2014	СПДС. Изображения условные графические электрооборудования и проводок на планах	
ГОСТ 2.306-68	ЕСКД. Обозначения графические материалов и правила их нанесения на чертежах	
	Прилагаемые документы	
ГД-2026-012-АИ.В1	Визуализация. Вид сверху (3D): планировка с мебелью, текстилем и декором	альбом визуализаций
ГД-2026-012-АИ.В2	Визуализация. Вид сверху (3D): планировка с мебелью, текстилем и декором	
ГД-2026-012-АИ.В3	Визуализация. Визуализация «room-bath-wide»	
ГД-2026-012-АИ.В4	Визуализация. Визуализация «room-bedroom-wC»	
ГД-2026-012-АИ.В5	Визуализация. Визуализация «room-bedroom-wD»	
ГД-2026-012-АИ.В6	Визуализация. Визуализация «room-corridor1-wB»	
ГД-2026-012-АИ.В7	Визуализация. Визуализация «room-corridor2-wide»	
ГД-2026-012-АИ.В8	Визуализация. Визуализация «room-corridor3-wide»	
ГД-2026-012-АИ.В9	Визуализация. Визуализация «room-hall-wA»	
ГД-2026-012-АИ.В10	Визуализация. Визуализация «room-hall-wB»	
ГД-2026-012-АИ.В11	Визуализация. Визуализация «room-kids1-wA»	
ГД-2026-012-АИ.В12	Визуализация. Визуализация «room-kids1-wC»	
ГД-2026-012-АИ.В13	Визуализация. Визуализация «room-kids2-wA»	
ГД-2026-012-АИ.В14	Визуализация. Визуализация «room-kids2-wD»	
ГД-2026-012-АИ.В15	Визуализация. Визуализация «room-living-wA»	
ГД-2026-012-АИ.В16	Визуализация. Визуализация «room-living-wB»	

Допущения и предложения на листе

Основа листа: взаимное расположение помещений, контур дома 9600 × 8000 и раскладка этажей подобраны проектировщиком под габариты помещений брифа; обмер и проект АР — задание (К-1); высота потолка 2900 мм — по брифу, не замерена; перекрытие 330 мм и отметка 2-го этажа +3,230 приняты; проект КР — задание (К-2); наружные стены 400 мм, перегородки 120 мм приняты (в брифе толщин нет) (К-1); разрешённая мощность 15 кВт принята по типовым ТУ для частного дома (К-4).
См. лист открытых вопросов (лист 6, записи К-1, К-2, К-4).

Общие указания — лист 5: ±0,000 — чистый пол; несущие конструкции и сети дома — по отдельному проекту; скрытые работы — по актам. Открытые вопросы и допущения — лист 6.

Изм.	Кол.уч	Лист	№ док.	Подп.	Дата
Разраб.		Кырлан А.С.			19.10.26
Пров.					
ГИП					
Н. контр.					
Утв.					

ГД-2026-012-АИ

Дом 120 м²

Общая площадь 147,36* м² · * размеры приняты, не замерены (реестр — л. 6, К-1)

Дизайн-проект интерьера

Стадия	Лист	Листов
РП	4	130

Общие данные

М б/м

Кырлан Александр Сергеевич

выпуск 19.10.2026 № 53e4f7ddae · стр. 6 из 160

Общие данные

Комплект ГД-2026-012-АИ · лист 4 общих данных (продолжение)

Ведомость ссылочных и прилагаемых документов (продолжение)

Обозначение	Наименование	Примечание
ГД-2026-012-АИ.В17	Визуализация. Визуализация «room-living-wC»	
ГД-2026-012-АИ.В18	Визуализация. Визуализация «room-storage-wide»	
ГД-2026-012-АИ.В19	Визуализация. Визуализация «room-study-wA»	
ГД-2026-012-АИ.В20	Визуализация. Визуализация «room-study-wC»	
ГД-2026-012-АИ.В21	Визуализация. Визуализация «room-wardrobe-wide»	
ГД-2026-012-АИ.В22	Визуализация. Визуализация «room-wc-wide»	

Состав дизайн-проекта

Раздел	Состав	Листы
Обложка	Дизайн-проект интерьера; Дом 120 м²; автор проекта — Кырлан Александр Сергеевич	1 с.
Концепция	Стиль Средиземноморский 60 % + Скандинавский 40 %: концепция интерьера, палитра и материалы (колерная карта — лист 62)	л. 20
Визуализации	22 изобр.: Вид сверху (3D): планировка с мебелью, текстилем и декором; Вид сверху (3D): планировка с мебелью, текстилем и декором; Визуализация «room-bath-wide»; Визуализация «room-bedroom-wC»; Визуализация «room-bedroom-wD»; Визуализация «room-corridor1-wB»; Визуализация «room-corridor2-wide»; Визуализация «room-corridor3-wide»; Визуализация «room-hall-wA»; Визуализация «room-hall-wB»; Визуализация «room-kids1-wA»; Визуализация «room-kids1-wC»; Визуализация «room-kids2-wA»; Визуализация «room-kids2-wD»; Визуализация «room-living-wA»; Визуализация «room-living-wB»; Визуализация «room-living-wC»; Визуализация «room-storage-wide»; Визуализация «room-study-wA»; Визуализация «room-study-wC»; Визуализация «room-wardrobe-wide»; Визуализация «room-wc-wide»	В1–В22
Рабочие чертежи	планы, развёртки, узлы (развёртки и узлы — листы 94, 99, 101–111, 113, 114, 116–118, 123)	л. 1–130
Спецификации и ведомости	оборудование, изделия, отделка, электроточки	л. 17, 18, 24–27, 34, 35, 50, 51, 60–66, 71–73, 124–128

Условные обозначения

- контрольный отрезок 1000 мм натуры: по нему проверяют печать 1:1
- отметка уровня, м: ±0,000 — чистый пол жилых помещений
- (A) марка развёртки: буква стены, стрелка — взгляд
- (О1) марка отделки по реестру отделки альбома
- выноска узла: над полкой — узел, под полкой — лист

Допущения и предложения на листе

Основа листа: взаимное расположение помещений, контур дома 9600 × 8000 и раскладка этажей подобраны проектировщиком под габариты помещений брифа; обмер и проект АР — задание (К-1); высота потолка 2900 мм — по брифу, не замерена; перекрытие 330 мм и отметка 2-го этажа +3,230 приняты; проект КР — задание (К-2); наружные стены 400 мм, перегородки 120 мм приняты (в брифе толщин нет) (К-1); разрешённая мощность 15 кВт принята по типовым ТУ для частного дома (К-4).
См. лист открытых вопросов (лист 6, записи К-1, К-2, К-4).

Общие указания

1. Рабочие чертежи интерьера разработаны на основании задания на проектирование и обмерного плана (лист 13). Объект: Дом 120 м²; автор проекта — Кырлан Александр Сергеевич; общая площадь 147,36 м², жилая 81,02 м², помещений 13.
2. Рабочие чертежи выполнены в соответствии с заданием на проектирование и нормативными документами, перечисленными в п. 4.
3. Открытые вопросы, принятые допущения и конфликты между разделами, не снятые к выпуску комплекта, сведены в таблицы на листе 6. До ответа по пункту таблицы показанное на указанном там листе — допущение, а не утверждённое решение: комплект по этим листам предварительный.
4. Нормативные документы, на которые есть ссылки в листах комплекта: ГОСТ Р 21.101-2026; ГОСТ 21.501-2018; ГОСТ 2.302-68; ГОСТ 2.303-68; ГОСТ 2.304-81; ГОСТ 2.307-2011; СП 54.13330.2022; СП 71.13330.2017; СП 73.13330.2016; ПУЭ (7-е изд.), гл. 1.8, 7.1; ГОСТ Р 50571.7.701-2024; СанПиН 1.2.3685-21; ГОСТ 2.702; ГОСТ 2.755; ГОСТ 21.110-2013; ГОСТ 13996-2019; ГОСТ 25772-2025; ГОСТ 31565-2012; ГОСТ 31975; ГОСТ 32414-2013; ГОСТ 32415-2013; ГОСТ Р 56387-2018; СП 20.13330.2016; СП 29.13330.2011; СП 55.13330.2016; СП 59.13330.2020. Документы из ведомости ссылочных документов здесь не повторяются.
5. За отметку ±0,000 принят уровень чистого пола жилых помещений квартиры (относительная отметка; абсолютная — по проекту дома). Отметка чистого пола мокрых помещений — −0,015. Размеры — в миллиметрах, отметки — в метрах, площади — в м²; высоты установки Н от чистого пола своего помещения до оси изделия.
6. Несущие конструкции, общедомовые стояки, вентиляционные каналы и инженерные сети дома настоящим комплектом не изменяются. Работы, затрагивающие их (проём или штраба в несущей стене, перенос стояка, врезка в вентканал, расширение мокрой зоны), выполняются только по отдельному проекту, к которому прилагается техническое заключение о допустимости и безопасности работ, выданное автором проекта дома или организацией с допуском на обследование, и который согласован в установленном порядке (Жилищный кодекс РФ, ст. 25–29).
7. Трассы инженерных сетей на листах — принципиальные. Расчёты электрических нагрузок и токов КЗ, гидравлики, воздухообмена, освещённости и нагрузок на перекрытие выполняются в проектах ЭОМ, ВК, ОВ и КР организацией с допуском СРО; фактические трассы до закрытия отделкой фиксируются исполнительными схемами.
8. Стиль интерьера — Средиземноморский 60 % + Скандинавский 40 %. Палитра проекта: основной 60 % — Tikkurila G503 «Calla», Farrow & Ball No. 239 «Wimborne White — белый с каплей тёплой охры», Little Greene No. 222 «Loft White»; дополнительный 30 % — NCS S 1010-Y20R «Светлый песок / известняк», Farrow & Ball No. 89 «Lulworth Blue — светлая морская лазурь», Farrow & Ball No. 292 «Treron — серо-оливковая листва»; акцент 10 % — NCS S 3050-R80B «Эгейский синий», Farrow & Ball No. 66 «India Yellow — охра / горчица итальянских фасадов», NCS S 5020-G90Y «Олива». Коды цвета — по веерам производителей; цвет утверждается по выкрасу на объекте при освещении проекта.
9. Площади поверхностей — по чистым граням стен до отделки: стены = периметр × высоту от чистого пола помещения до низа потолка минус проёмы (облицовка плиткой — до верха облицовки); плинтус = периметр минус дверные проёмы; пол и потолок — по площади помещения. Количество плиток — по раскладке. Способ один для всех листов комплекта (ведомость отделки, колерная карта, раскладка плитки, развёртки).
10. Марки: стены помещения на всех листах — А (верхняя по плану), Б (правая), В (нижняя), Г (левая); марка отделки О — одна на весь альбом; реестр марок отделки (с позициями колерной карты той же отделки) и марки позиций по видам — на листе 92.
11. Развёртки стен выполнены по всем помещениям для стен с электроточками, мебелью, декором и отделкой: санузлы и кухонный фронт — в М 1:25, остальные стены — в М 1:40; расположение развёрток и узлов — на листе 94, узлы — на листе 123.
12. Перечень скрытых работ, на которые составляются акты освидетельствования (форма по приказу Минстроя России № 344/пр): гидроизоляция пола и стен мокрых помещений (с тестом проливом); стяжка пола (толщина, прочность, влажность основания); скрытая электропроводка (за потолком и в штробах стен; условия штробления — в следующем пункте); трубопроводы водоснабжения и канализации до закрытия (опрессовка, уклоны); закладные и усиления под подвесные приборы, мебель и тяжёлый декор, рамы инсталляций; короба дверей скрытого монтажа до штукатурки; каркасы ГКЛ потолков, коробов и перегородок до обшивки.
13. Скрытая электропроводка: за потолком и в штробах стен. Штробы в стенах выполняются только после технического заключения о несущих конструкциях; до заключения несущие стены не определены, и все стены считаются несущими; объём штроб — в ведомости объёмов работ, строка «Штробы в стенах» (вертикальные спуски; объём не меньше фактического, горизонтальные трассы — по исполнительной схеме).
14. Критерии приёмки: допуски отделочных покрытий — по СП 71.13330.2017; испытания систем водоснабжения и канализации — по СП 73.13330.2016 до закрытия трасс; приёмо-сдаточные испытания электроустановки — по ПУЭ, гл. 1.8, с протоколом электролаборатории.
15. Осознанные отступления от ГОСТ Р 21.101-2026, принятые в комплекте: номер листа и число листов («Листов») указаны на каждом листе; на масштабных листах в основной надписи указан фактический масштаб и дан контрольный отрезок 1000 мм; развёртки стен выполнены в М 1:25 и 1:40 (ГОСТ 21.507-81 — 1:50…1:500) ради читаемости привязок; размерные числа и марки элементов (Д-1, ОК-1, О6) — кеглем 2,5 мм, номера помещений — в кружке Ø 8 мм (канон — 3,5 мм и Ø 12 мм): так насыщенные листы А3 читаются без наложений надписей.
16. Графы «Пров.», «Н. контр.», «Утв.» основной надписи заполняются при согласовании комплекта с заказчиком; до согласования комплект подписывает автор проекта (графа «Разраб.»).

Изм.	Кол.уч	Лист	№ док.	Подп.	Дата	ГД-2026-012-АИ			
						Дом 120 м²			
						Общая площадь 147,36* м² · * размеры приняты, не замерены (реестр — л. 6, К-1)			
Разраб.		Кырлан А.С.			19.10.26	Дизайн-проект интерьера	Стадия	Лист	Листов
Пров.							РП	5	130
ГИП									
						Общие данные	**Кырлан Александр Сергеевич**		
Н. контр.						М б/м			
Утв.									

выпуск 19.10.2026 № 53e4f7ddae · стр. 7 из 160

Открытые вопросы, принятые допущения и конфликты

Сводка по реестрам координации (стартовое совещание 19.10.2026)

Комплект предварительный по пунктам этих таблиц. Пока по пункту нет ответа или решения, показанное на указанном листе — допущение проектировщика, а не утверждённое решение.
Сводка: открытых вопросов — 6 (из них ждут факта объекта — 2: контрольного обмера, обследования или документа).
Пункты, ответ на которые лежит на объекте, а не за столом проектировщика (графа «Вид», строка «Ждёт»), собраны на листе «Задание на контрольный обмер и обследование» (листы 7–9): что и где замерить, с какой точностью и чем подтвердить. Пункты, ждущие решения человека, на объекте не закрываются.

Открытые вопросы и принятые допущения

№	Формулировка	Вид	Кто решает	Если решения нет	Лист, где это проявляется
К-1	Бриф задаёт 11 помещений с габаритами и этажами, но не их взаимное расположение, контур дома и толщины стен: раскладка этажей, контур 9600 × 8000 и перегородки подобраны проектировщиком под габариты брифа. До заказа мебели, дверей и материалов нужен обмер или проект дома (АР).	Отсутствует Ждёт: обмера	Архитектор-планировщик	размеры на листах — предложение проектировщика по брифу, уточняются по месту; мебель на заказ и материалы по ним не заказывать	л. 13, 14 — Обмерный план л. 13–18, 20–23, 28–33, 38–49, 52, 53, 57–59, 62, 63, 68, 69, 74, 75, 114–116, 119–122 — 1-й этаж л. 22, 23 — План расстановки мебели л. 13–18, 20–23, 28–33, 38–49, 52, 53, 57–59, 62, 63, 68, 69, 74, 75, 114–116, 119–122 — 1-й этаж
К-2	Высота потолка 2900 мм — по брифу (не замерена); конструкция и толщина перекрытия не заданы — принято 330 мм с полом, отметка чистого пола 2-го этажа +3,230. Нужен проект КР дома.	Отсутствует	Архитектор-планировщик	высоты на развёртках, отметка 2-го этажа и лестница — от принятых 2900 / +3,230, уточнить по проекту КР	л. 13, 14 — Обмерный план л. 13–18, 20–23, 28–33, 38–49, 52, 53, 57–59, 62, 63, 68, 69, 74, 75, 114–116, 119–122 — 1-й этаж л. 52, 53 — План потолков л. 13–18, 20–23, 28–33, 38–49, 52, 53, 57–59, 62, 63, 68, 69, 74, 75, 114–116, 119–122 — 1-й этаж
К-3	Лестница по брифу — из холла 1-го этажа; место, тип (одномаршевая прямая, 17 подъёмов 190 × 250, марш 1000), конструкция и ограждение — предложение проектировщика. Расчёт несущей конструкции марша и проёма в перекрытии — проект КР.	Отсутствует	Архитектор-планировщик	лестница на планах — предложение, к изготовлению не выдаётся до проекта КР	л. 13, 14 — Обмерный план л. 13–18, 20–23, 28–33, 38–49, 52, 53, 57–59, 62, 63, 68, 69, 74, 75, 114–116, 119–122 — 1-й этаж
К-4	Разрешённая мощность дома по ТУ неизвестна, принята 15 кВт.	Отсутствует	Инженер-электрик	щит и группы рассчитаны на 15 кВт; при других ТУ пересчёт	л. 36 — Однолинейная схема щита л. 28, 29 — План розеток и электровыводов л. 13–18, 20–23, 28–33, 38–49, 52, 53, 57–59, 62, 63, 68, 69, 74, 75, 114–116, 119–122 — 1-й этаж
К-5	Тип дома, материал и конструкция стен и перекрытия, несущие стены, положение стояков и выпусков канализации в брифе не заданы; проект дома (АР, КР, ВК) не передан. Стояки на планах показаны по предложению проектировщика.	Отсутствует Ждёт: документа	Архитектор-планировщик	все существующие стены считаются несущими: проёмы и перегородки — предложение, к строительству не выдаются; стояки — предложение	л. 13, 14 — Обмерный план л. 13–18, 20–23, 28–33, 38–49, 52, 53, 57–59, 62, 63, 68, 69, 74, 75, 114–116, 119–122 — 1-й этаж л. 48, 49 — Схема разводки водопровода и канализации л. 13–18, 20–23, 28–33, 38–49, 52, 53, 57–59, 62, 63, 68, 69, 74, 75, 114–116, 119–122 — 1-й этаж
К-6	Источник отопления и горячей воды (котёл: газ / электро, его место, котельная) брифом не задан; в составе помещений брифа котельной нет. Отопительные приборы на листах — водяные радиаторы под окнами при любом источнике тепла.	Решение	Инженер ОВ	радиаторы и трассы — предложение; котёл, котельная и ввод газа — после ответа заказчика	л. 44, 45 — План отопления л. 13–18, 20–23, 28–33, 38–49, 52, 53, 57–59, 62, 63, 68, 69, 74, 75, 114–116, 119–122 — 1-й этаж л. 48, 49 — Схема разводки водопровода и канализации л. 13–18, 20–23, 28–33, 38–49, 52, 53, 57–59, 62, 63, 68, 69, 74, 75, 114–116, 119–122 — 1-й этаж

Примечания

1. Номера листов — по ведомости рабочих чертежей комплекта (лист «Общие данные»).
2. Графа «Если решения нет» показывает состояние решения на листах; влияние на сроки и стоимость по пунктам не оценивалось.
3. Пункт, по которому принято решение, при следующем выпуске комплекта из таблиц исключается.

Изм.	Кол.уч	Лист	№ док.	Подп.	Дата
Разраб.		Кырлан А.С.			19.10.26
Пров.					
ГИП					
Н. контр.					
Утв.					

ГД-2026-012-АИ

Дом 120 м²

Общая площадь 147,36* м² · * размеры приняты, не замерены (реестр — л. 6, К-1)

Дизайн-проект интерьера

Стадия	Лист	Листов
РП	6	130

Открытые вопросы, принятые допущения и конфликты
М б/м

Кырлан Александр Сергеевич

Задание на контрольный обмер и обследование. Лист 1 из 3

ПРЕДВАРИТЕЛЬНО · не для производства работ · открыто пунктов: 6 (реестр — л. 6)

Что замерить, вскрыть и получить до заказа материалов и изделий

Задание собрано из открытых вопросов, ответ на которые лежит на объекте или в документах, а не за столом проектировщика. Пока факт не получен, размер, материал или положение на листах — допущение (знак «*»), а не замер.
Сводка: на объекте — 7 (до демонтажа — 5; после демонтажа — 2); документом и при закупке — 2; из допущений в данных и на листах — 8, из них без вопроса в реестре — 5. Закрываются вопросы: К-1, К-2, К-4, К-5 (4). Вопросы, ждущие решения человека, задание не закрывает — они решаются по реестру открытых вопросов.

Условия проведения

Порядок работ	Приёмы и точность	Кто присутствует	Если факт не совпал с проектом
1. До демонтажа — существующее состояние: контур, диагонали, высоты, проёмы, оси стояков, ниши и конструкции, которые видны. 2. После демонтажа, до черновых работ — то, что закрывали отделка и короба: основание стен, фактические толщины, углы, узлы. 3. Документы и данные закупки — не на объекте: к сроку из последней таблицы, от них зависят привязки и заказ. Что заказывается по размеру из задания, до закрытия пункта не заказывают: сроки изготовления — по графику закупок прораба.	Обход по часовой стрелке от входа: стены, проёмы, потолок, коммуникации (стояки, щиток, вентканалы), особенности (ниши, короба, выступы). Размеры записывают в мм; сумма участков равна общему размеру, при цепочке длиннее трёх участков ставят проверочный (общий) размер. Диагонали каждого помещения; если две диагонали различаются на 5 мм и больше, разницу подписывают на плане. Потолок — в нескольких точках: центр, углы, у проёмов. Проём — ширина, высота, глубина откоса, привязка к ближайшим углам, высота подоконника. Допустимая погрешность прибора — 2–3 мм на метр; размеры округляют кратно 5 мм; два контрольных промера одного размера не должны расходиться более чем на 2 %. Допуск по пункту — в графе «Точность». План БТИ обмер не заменяет.	Прораб (отвечает за проведение) — назначает день и порядок обхода, открывает объект и освобождает помещения, ведёт это задание и реестр изменений. Архитектор — выполняет обмер, составляет акт контрольного обмера и подписывает результаты по размерам и конструкциям. Владельцы вопросов присутствуют при пунктах своего раздела или принимают результат до заказа: Инженер ВК (вода, канализация) позиции О-1; Инженер-электрик — К-4; позиции О-2; Инженер ОВ позиции О-3; Отделочник — позиции О-6, О-7. Заказчик или его представитель — передаёт документы (план БТИ, проект дома, технические условия, паспорта), подписывает акт. Проектных решений на обмере не принимают: обмер даёт факт, решения — по реестру открытых вопросов (лист 6).	1. В пределах допуска пункта — принимается измеренное значение, лист перевыпускается, знак «*» снимается. 2. Больше допуска или контрольные промеры расходятся более чем на 2 % — промер повторяют; не подтвердилось — запись в реестр изменений (дата, лист, было, стало, кто решил, подпись), работы в этом месте не начинают. 3. Затронуты несущая стена, стояк, вентканал или мокрая зона — сразу владельцу раздела и ГИПу (главному инженеру проекта); между разделами не больше двух кругов, затем решает ГИП. 4. На объекте устно ничего не согласуется: каждое решение — записью в реестр с подписью.

Этап 1. До демонтажа

№	Где	Способ	Что сделать	Кто выполняет	Точность	Что пересчитается в альбоме	Чем подтверждается	Закрывает вопросы реестра
О-1	Ввод В1 и Т3 у стояков; по всей квартире	Обмер	Отключающая арматура и счётчики воды на вводах: положение, тип, пломбы управляющей компании. Альбом ставит их на каждом вводе по практике, в данных их нет.	Архитектор	±5 мм	Узлы ввода в спецификации ВК (краны, фильтры, счётчики); места ввода на плане выводов. Листы: л. 46, 47 — План выводов сантехники л. 50 — Спецификация сантехнического оборудования	акт контрольного обмера; фото с рулеткой и привязкой к стене или углу	Вопроса в реестре нет: Альбом принимает счётчики воды на вводах без осмотра. Результат принимает: Инженер ВК (вода, канализация)
О-2	Вход в квартиру или лестничная клетка; место щита на плане	Обмер	Существующий щиток и счётчик электроэнергии: место и габарит ниши, состояние ввода, марка и сечение вводного кабеля, наличие вводного автомата и УЗО, пломбы.	Архитектор	±5 мм	Ниша и место щита на листах; вводной кабель и аппараты на однолинейной схеме; расстояния до первых групп. Листы: л. 36, 37 — Однолинейная схема щита	акт контрольного обмера; фото с рулеткой и привязкой к стене или углу	Вопроса в реестре нет: Альбом принимает щит и ввод без осмотра. Результат принимает: Инженер-электрик
О-3	у окон	Обмер	Положение стояков отопления (подающий и обратный) от граней стен, диаметры, наличие запорной арматуры; существующие радиаторы: число секций, межосевое расстояние, подводки. В данных стояков отопления нет — лист отопления выводит их условно у откоса окна.	Архитектор	±5 мм	План отопления: места стояков и подводок, привязки радиаторов; подбор радиаторов по теплотехническому расчёту; радиаторы и узлы подключения в ВОР и спецификации. Листы: л. 44, 45 — План отопления	акт контрольного обмера; фото с рулеткой и привязкой к стене или углу	Вопроса в реестре нет: Альбом принимает положение стояков и радиаторов отопления без обмера. Результат принимает: Инженер ОВ
О-4	все помещения	Обмер	Обмер всех помещений обоих этажей: стороны, диагонали, проёмы, высота потолка, проём лестницы.	исполнитель	±5 мм; диагонали — разница от 5 мм подписывается	обмерный и монтажный планы, развёртки, мебель на заказ Листы: л. 13, 14 — Обмерный план л. 13–18, 20–23, 28–33, 38–49, 52, 53, 57–59, 62, 63, 68, 69, 74, 75, 114–116, 119–122 — 1-й этаж л. 22, 23 — План расстановки мебели	акт контрольного обмера	К-1 Результат принимает: Архитектор

Допущения и предложения на листе
Основа листа: взаимное расположение помещений, контур дома 9600 × 8000 и раскладка этажей подобраны проектировщиком под габариты помещений брифа; обмер и проект АР — задание (К-1); высота потолка 2900 мм — по брифу, не замерена; перекрытие 330 мм и отметка 2-го этажа +3,230 приняты; проект КР — задание (К-2); наружные стены 400 мм, перегородки 120 мм приняты (в брифе толщин нет) (К-1); разрешённая мощность 15 кВт принята по типовым ТУ для частного дома (К-4).
См. лист открытых вопросов (лист 6, записи К-1, К-2, К-4).

Изм.	Кол.уч	Лист	№ док.	Подп.	Дата
Разраб.		Кырлан А.С.			19.10.26
Пров.					
ГИП					
Н. контр.					
Утв.					

ГД-2026-012-АИ

Дом 120 м²

Общая площадь 147,36* м² · * размеры приняты, не замерены (реестр — л. 6, К-1)

Дизайн-проект интерьера

Стадия	Лист	Листов
РП	7	130

Задание на контрольный обмер и обследование.
Лист 1 из 3
М б/м

Кырлан Александр Сергеевич

выпуск 19.10.2026 № 53e4f7ddae · стр. 9 из 160

Задание на контрольный обмер и обследование. Лист 2 из 3

ПРЕДВАРИТЕЛЬНО · не для производства работ · открыто пунктов: 6 (реестр — л. 6)

Что замерить, вскрыть и получить до заказа материалов и изделий

Этап 1. До демонтажа (продолжение)

№	Где	Способ	Что сделать	Кто выполняет	Точность	Что пересчитается в альбоме	Чем подтверждается	Закрывает вопросы реестра
О-5	Все помещения квартиры	Обмер	Высота потолка в каждом помещении в нескольких точках: центр, углы, у проёмов.	Архитектор	±5 мм	Вертикальные размеры альбома: развёртки, шкафы, плитка, объёмы работ. Листы: л. 2–5 — Общие данные	акт контрольного обмера	К-2 Результат принимает: Архитектор

Этап 2. После демонтажа, до черновых работ

№	Где	Способ	Что сделать	Кто выполняет	Точность	Что пересчитается в альбоме	Чем подтверждается	Закрывает вопросы реестра
О-6	Гостиная-кухня (пом. 1), Холл с лестницей (пом. 2), Кабинет (пом. 3), Санузел гостевой (пом. 4), Прихожая (пом. 5), Спальня родителей (пом. 6), Детская (пом. 7), Гардеробная (пом. 8), Кладовая (пом. 9), Холл второго этажа (пом. 10), Коридор второго этажа (пом. 11), Детская вторая (пом. 12), Санузел второго этажа (пом. 13)	Обмер	Нивелировка плиты перекрытия и существующего пола после демонтажа покрытий: отметки в углах и по сетке, перепады по помещению, уклоны, отметки порогов (чистый пол в мокрых зонах принят -15 мм, 0 мм). Принятая толщина стяжки 33 мм, 50 мм и отметка чистого пола — расчётные, не от замера плиты.	Архитектор	±5 мм по отметке; ровность просвет под 2-метровой рейкой, горизонталь против 0,2 % длины помещения	Толщина стяжки и отметка чистого пола; уклоны к трапам и пороги; выпуски К1 относительно чистого пола (план разводки); объёмы стяжки и смеси в ВОР и спецификации. Листы: л. 54, 58, 59 — План полов л. 48, 49 — Схема разводки водопровода и канализации	акт контрольного обмера	Вопроса в реестре нет: Альбом принимает отметки плиты и толщину пирога пола без нивелировки. Результат принимает: Отделочник
О-7	Гостиная-кухня (пом. 1), Холл с лестницей (пом. 2), Кабинет (пом. 3), Санузел гостевой (пом. 4), Прихожая (пом. 5), Спальня родителей (пом. 6), Детская (пом. 7), Гардеробная (пом. 8), Кладовая (пом. 9), Холл второго этажа (пом. 10), Коридор второго этажа (пом. 11), Детская вторая (пом. 12), Санузел второго этажа (пом. 13)	Обмер	Вертикаль и плоскостность стен: отклонение от вертикали по высоте стены (отвес или лазерный уровень), просвет под правилом 2 м, кривизна углов. Нужно там, где от стены зависит изделие: облицовка плиткой (пом. 4, 13), штукатурка и окраска (пом. 1, 2, 3, 4, 5, 6, 7, 8, 9, 10, 11, 12, 13), встроенная мебель и кухня (пом. 1, 5, 6, 7, 12).	Архитектор	до 1 мм на 2 м (правило и клиновой щуп); вертикаль — мм на высоту стены, отклонения подписываются на плане	Толщина штукатурки и расход смеси в ВОР и спецификации; раскладка плитки (подрезка у стен); зазоры и крепление встроенной мебели и кухни. Листы: л. 54–57 — Раскладка плитки л. 60, 61 — Ведомость отделки помещений	акт контрольного обмера	Вопроса в реестре нет: Альбом принимает стены ровными и вертикальными без замера. Результат принимает: Отделочник

Документы и данные закупки (не на объекте)

№	У кого, откуда	Способ	Что получить	К какому сроку	Что пересчитается в альбоме	Чем подтверждается	Закрывает вопросы реестра
О-8	Заказчик; организация, выдавшая технические условия	Документ	Технические условия на присоединение: разрешённая мощность.	До утверждения однолинейной схемы щита	Однолинейная схема щита: вводной аппарат и группы. Листы: л. 2–5 — Общие данные	копия документа	К-4 Результат принимает: Инженер-электрик
О-9	заказчик	Документ	Проект дома (разделы АР, КР, ВК, ОВ) или обследование: несущие конструкции, перекрытие, стояки, вводы сетей.	до демонтажа и возведения перегородок	монтажный план, проёмы, стояки, развёртки Листы: л. 13, 14 — Обмерный план л. 13–18, 20–23, 28–33, 38–49, 52, 53, 57–59, 62, 63, 68, 69, 74, 75, 114–116, 119–122 — 1-й этаж л. 48, 49 — Схема разводки водопровода и канализации	копия документа	К-5 Результат принимает: Архитектор

Допущения и предложения на листе

Основа листа: взаимное расположение помещений, контур дома 9600 × 8000 и раскладка этажей подобраны проектировщиком под габариты помещений брифа; обмер и проект АР — задание (К-1); высота потолка 2900 мм — по брифу, не замерена; перекрытие 330 мм и отметка 2-го этажа +3,230 приняты; проект КР — задание (К-2); наружные стены 400 мм, перегородки 120 мм приняты (в брифе толщин нет) (К-1); разрешённая мощность 15 кВт принята по типовым ТУ для частного дома (К-4).

См. лист открытых вопросов (лист 6, записи К-1, К-2, К-4).

Изм.	Кол.уч	Лист	№ док.	Подп.	Дата
Разраб.		Кырлан А.С.			19.10.26
Пров.					
ГИП					
Н. контр.					
Утв.					

ГД-2026-012-АИ

Дом 120 м²

Общая площадь 147,36* м² · * размеры приняты, не замерены (реестр — л. 6, К-1)

Дизайн-проект интерьера

Стадия	Лист	Листов
РП	8	130

Задание на контрольный обмер и обследование.
Лист 2 из 3
М б/м

Кырлан Александр Сергеевич

Задание на контрольный обмер и обследование. Лист 3 из 3

Что замерить, вскрыть и получить до заказа материалов и изделий

Примечания

1. Подтверждение: акт контрольного обмера (дата, кто присутствовал, прибор, перечень промеров с результатами, подписи присутствующих); к акту — фото вскрытий и узлов и техническое заключение организации, выполнившей обследование.
2. Номера листов — по ведомости рабочих чертежей комплекта (лист «Общие данные»).
3. Пункт исключается из задания при следующем выпуске, когда акт подписан, значение внесено в проект и листы перевыпущены; знак «*» у величины снимается только замером.

Допущения и предложения на листе

Основа листа: взаимное расположение помещений, контур дома 9600 × 8000 и раскладка этажей подобраны проектировщиком под габариты помещений брифа; обмер и проект АР — задание (К-1); высота потолка 2900 мм — по брифу, не замерена; перекрытие 330 мм и отметка 2-го этажа +3,230 приняты; проект КР — задание (К-2); наружные стены 400 мм, перегородки 120 мм приняты (в брифе толщин нет) (К-1); разрешённая мощность 15 кВт принята по типовым ТУ для частного дома (К-4).
См. лист открытых вопросов (лист 6, записи К-1, К-2, К-4).

Изм.	Кол.уч	Лист	№ док.	Подп.	Дата
Разраб.		Кырлан А.С.			19.10.26
Пров.					
ГИП					
Н. контр.					
Утв.					

ГД-2026-012-АИ

Дом 120 м²

Общая площадь 147,36* м² · * размеры приняты, не замерены (реестр — л. 6, К-1)

Дизайн-проект интерьера

Стадия	Лист	Листов
РП	9	130

Задание на контрольный обмер и обследование.
Лист 3 из 3
М б/м

Кырлан Александр Сергеевич

выпуск 19.10.2026 № 53e4f7ddae · стр. 11 из 160

График закупок и работ. Лист 1 из 3

ПРЕДВАРИТЕЛЬНО · не для производства работ · открыто пунктов: 6 (реестр — л. 6)

Что заказывать и когда не раньше чего: относительный порядок без дат; срок поставки — из данных или «уточняется у поставщика»

Лист не содержит дат: контрольного обмера, подписанных решений автора и договоров ещё нет, и любая дата была бы выдумана. Вместо календаря — порядок и условия: замер → решение и выбор изделия → заказ → срок поставки → работа, которую позиция блокирует. Срок поставки печатается как срок, только если он задан в данных позиции. Нет — «срок уточняется у поставщика» и ссылка на вопрос реестра о сроках; типовой диапазон практики стоит рядом как ориентир и заказывать по нему нельзя. Номера З-N и Р-N — строки этого листа, К-N — записи реестра открытых вопросов, О-N — позиции задания на контрольный обмер.

Закупки: что заказывается, от чего зависит заказ и какую работу блокирует

№	Позиция и где	1. Замер до заказа	2. Решение, выбор изделия, паспорт	3. Условие заказа	4. Срок поставки	5. Блокирует работу	Закрывает вопросы реестра
З-1	Двери скрытого монтажа с коробом под покраску в существующих проёмах: Д-1, Д-2, Д-3, Д-4, Д-5, Д-6, Д-7, Д-10, Д-9, Д-8 — 10 шт. пом. 1, 3, 4, 5, 6, 7, 8, 9, 12, 13	О-4: обмер: все помещения (К-1); до заказа мебели и дверей		После 1 и 2 и после получения срока у поставщика (вопроса о сроках нет); дата заказа — когда срок известен, не позднее чем за срок до начала Р-5.	срок уточняется у поставщика Ориентир практики (не срок поставщика): ≈ 30 дн.	Р-5 «штукатурка»: короб ставят до штукатурки (коробку ставят на черновой стадии; полотно навешивают после чистовой отделки стен)	К-1
З-2	Кухонный гарнитур по проекту кухни: модули Кх1, Кх2, Кх3, Кх4, Кх5, Кх6, Кх7, Кх8, Кх9, Кх10, Кх11, Кх12, Кх13, Кх14 пом. 1			После 1 и 2 и после получения срока у поставщика (вопроса о сроках нет); дата заказа — когда срок известен, не позднее чем за срок до начала Р-15.	срок уточняется у поставщика Ориентир практики (не срок поставщика): 4–8 нед. от замера	Р-15 «кухня и мебель»: замер кухни — по готовым стенам после штукатурки или плитки, до чистового пола; производство идёт параллельно со стяжкой и отделкой	
З-3	Встраиваемая техника кухни: Кх3 посудомоечная машина, Кх9 холодильник пом. 1			После 1 и 2 и после получения срока у поставщика (вопроса о сроках нет); дата заказа — когда срок известен, не позднее чем за срок до начала Р-15.	срок уточняется у поставщика	Р-15 «кухня и мебель»: паспорта и монтажные схемы — до изготовления модулей кухни: нишу и вентзазоры задаёт модель, а не типовая схема 60 см	
З-4	Стиральная машина: См3 (вертикальная загрузка 400 × 600 мм — условие закупки) пом. 13			После 1 и 2 и после получения срока у поставщика (вопроса о сроках нет); дата заказа — когда срок известен, не позднее чем за срок до начала Р-4.	срок уточняется у поставщика	Р-4 «черновая сантехника»: габарит и подводка — до закрытия люка и разводки	
З-5	Сантехнические приборы и инсталляции: Ст1, Ст2, См1, См2, См4 пом. 4, 13	О-3: обмер: у окон		После 1 и 2 и после получения срока у поставщика (вопроса о сроках нет); дата заказа — когда срок известен, не позднее чем за срок до начала Р-4.	срок уточняется у поставщика	Р-4 «черновая сантехника»: инсталляцию ставят до обшивки ГКЛВ и до гидроизоляции стены	
З-6	Керамогранит и плитка: 4 поз. по артикулу и формату, 61,69 м² по раскладке пом. 1, 4, 5, 13	О-6: обмер: Гостиная-кухня (пом. 1), Холл с лестницей (пом. 2), Кабинет (пом. 3), Санузел гостевой (пом. 4), Прихожая (пом. 5), Спальня родителей (пом. 6), Детская (пом. 7), Гардеробная (пом. 8), Кладовая (пом. 9), Холл второго этажа (пом. 10), Коридор второго этажа (пом. 11), Детская вторая (пом. 12), Санузел второго этажа (пом. 13) О-7: обмер: Гостиная-кухня (пом. 1), Холл с лестницей (пом. 2), Кабинет (пом. 3), Санузел гостевой (пом. 4), Прихожая (пом. 5), Спальня родителей (пом. 6), Детская (пом. 7), Гардеробная (пом. 8), Кладовая (пом. 9), Холл второго этажа (пом. 10), Коридор второго этажа (пом. 11), Детская вторая (пом. 12), Санузел второго этажа (пом. 13)		После 1 и 2 и после получения срока у поставщика (вопроса о сроках нет); дата заказа — когда срок известен, не позднее чем за срок до начала Р-9.	срок уточняется у поставщика	Р-9 «плитка»: калибр партии измеряют до раскладки, раскладку пересчитывают до заказа	

Допущения и предложения на листе

Основа листа: взаимное расположение помещений, контур дома 9600 × 8000 и раскладка этажей подобраны проектировщиком под габариты помещений брифа; обмер и проект АР — задание (К-1); высота потолка 2900 мм — по брифу, не замерена; перекрытие 330 мм и отметка 2-го этажа +3,230 приняты; проект КР — задание (К-2); наружные стены 400 мм, перегородки 120 мм приняты (в брифе толщин нет) (К-1); разрешённая мощность 15 кВт принята по типовым ТУ для частного дома (К-4).
См. лист открытых вопросов (лист 6, записи К-1, К-2, К-4).

Изм.	Кол.уч	Лист	№ док.	Подп.	Дата
Разраб.		Кырлан А.С.			19.10.26
Пров.					
ГИП					
Н. контр.					
Утв.					

ГД-2026-012-АИ

Дом 120 м²

Общая площадь 147,36* м² · * размеры приняты, не замерены (реестр — л. 6, К-1)

Дизайн-проект интерьера

Стадия	Лист	Листов
РП	10	130

График закупок и работ. Лист 1 из 3

М б/м

Кырлан Александр Сергеевич

выпуск 19.10.2026 № 53e4f7ddae · стр. 12 из 160

График закупок и работ. Лист 2 из 3

Что заказывать и когда не раньше чего: относительный порядок без дат; срок поставки — из данных или «уточняется у поставщика»

Закупки: что заказывается, от чего зависит заказ и какую работу блокирует (продолжение)

№	Позиция и где	1. Замер до заказа	2. Решение, выбор изделия, паспорт	3. Условие заказа	4. Срок поставки	5. Блокирует работу	Закрывает вопросы реестра
З-7	Покрытие пола (доска) и плинтус: пом. 1, 2, 3, 6, 7, 8, 9, 10, 11, 12 пом. 1, 2, 3, 6, 7, 8, 9, 10, 11, 12	О-6: обмер: Гостиная-кухня (пом. 1), Холл с лестницей (пом. 2), Кабинет (пом. 3), Санузел гостевой (пом. 4), Прихожая (пом. 5), Спальня родителей (пом. 6), Детская (пом. 7), Гардеробная (пом. 8), Кладовая (пом. 9), Холл второго этажа (пом. 10), Коридор второго этажа (пом. 11), Детская вторая (пом. 12), Санузел второго этажа (пом. 13)		После 1 и 2 и после получения срока у поставщика (вопроса о сроках нет); дата заказа — когда срок известен, не позднее чем за срок до начала Р-12.	срок уточняется у поставщика	Р-12 «чистовые полы»: артикул и партия — до заказа; доску привозят к чистовым полам	
З-8	Встроенная мебель по замеру цеха: Пр1, М4, Д3, Д8 пом. 5, 6, 7, 12	О-4: обмер: все помещения (К-1); до заказа мебели и дверей		После 1 и 2 и после получения срока у поставщика (вопроса о сроках нет); дата заказа — когда срок известен, не позднее чем за срок до начала Р-15.	срок уточняется у поставщика Ориентир практики (не срок поставщика): 4–8 нед. от замера	Р-15 «кухня и мебель»: цех замеряет по готовым стенам; производство 4–8 недель идёт параллельно с отделкой	К-1

Работы: порядок и что не даёт начать

№	Работа (стадия технологической последовательности)	После	Что должно быть к началу: условия и закупки	Не начинать, пока открыто в реестре
Р-1	Демонтаж покрытий, отделки стен и потолков, дверных блоков и приборов; конструкции, стены и перегородки не трогать до технического заключения (стадия 1)		до начала: запрошены документы на дом и БТИ; контрольный обмер до демонтажа (что видно) сделан	
Р-2	Контрольный обмер на голых стенах и обследование (задание — лист «Задание на контрольный обмер») (стадия 2)	Р-1	после снятия отделки: видны стояки, каналы, щиток, толщины стен; до заказа всего, что делают по размеру	
Р-3	Черновая электрика: штробы, короба, гофра, подрозетники, щит (стадия 4)	Р-2	до начала: план электрики с высотами утверждён; штробы в стенах — только после технического заключения; мебель расставлена	К-4: Разрешённая мощность дома по ТУ неизвестна, принята 15 кВт.
Р-4	Черновая сантехника и вентиляция: разводка, выводы, инсталляции, короба стояков (стадия 5)	Р-2	до начала: положение стояков замерено; модели инсталляций и машины выбраны (габариты рамы, подводка); инсталляцию ставят до обшивки ГКЛВ и до гидроизоляции Закупки к началу: З-4 (стиральная машина), З-5 (сантехника)	
Р-5	Коробки скрытых дверей, затем штукатурка стен и откосов (стадия 6)	Р-2, Р-3, Р-4	до начала: электрика и сантехника смонтированы, штробы заделаны; коробки скрытых дверей установлены до штукатурки (поэтому заказ дверей — раньше работы) Закупки к началу: З-1 (двери скрытого монтажа)	К-1: Бриф задаёт 11 помещений с габаритами и этажами, но не их взаимное расположение, контур дома и толщины стен: раскладка этажей, контур 9600 × 8000 и перегородки подобраны проектировщиком под габариты брифа.
Р-6	Стяжка пола и тёплый пол (стадия 7)	Р-5	до начала: штукатурка сделана; трубы под стяжкой приняты; нивелировка плиты выполнена	
Р-7	Гидроизоляция санузлов и тест проливом (стадия 8)	Р-6	до начала: стяжка набрала прочность и сухая по инструкции гидроизоляции; выводы стоят на проектных отметках	
Р-8	ГКЛ: короба инсталляции и стояков, ниши, потолки (стадия 9)	Р-3, Р-4	до начала: черновые сети в зоне коробов приняты; закладные под тяжёлое и карнизы стоят; светильники выбраны (вырезы)	
Р-9	Плитка и керамогранит: стены, затем пол; фартук (стадия 10)	Р-6, Р-7, Р-8	до начала: гидроизоляция принята; плитка выбрана, калибр партии измерен, раскладка пересчитана и подписана Закупки к началу: З-6 (плитка)	
Р-10	Шпаклёвка стен и потолков под окраску (стадия 11)	Р-5, Р-8, Р-9	до начала: плитка готова (грязные работы закончены); штукатурка и ГКЛ сухие	

Допущения и предложения на листе

Основа листа: взаимное расположение помещений, контур дома 9600 × 8000 и раскладка этажей подобраны проектировщиком под габариты помещений брифа; обмер и проект АР — задание (К-1); высота потолка 2900 мм — по брифу, не замерена; перекрытие 330 мм и отметка 2-го этажа +3,230 приняты; проект КР — задание (К-2); наружные стены 400 мм, перегородки 120 мм приняты (в брифе толщин нет) (К-1); разрешённая мощность 15 кВт принята по типовым ТУ для частного дома (К-4).

См. лист открытых вопросов (лист 6, записи К-1, К-2, К-4).

Изм.	Кол.уч	Лист	№ док.	Подп.	Дата
Разраб.		Кырлан А.С.			19.10.26
Пров.					
ГИП					
Н. контр.					
Утв.					

ГД-2026-012-АИ

Дом 120 м²

Общая площадь 147,36* м² · * размеры приняты, не замерены (реестр — л. 6, К-1)

	Стадия	Лист	Листов
Дизайн-проект интерьера	РП	11	130

График закупок и работ. Лист 2 из 3

М 6/м

Кырлан Александр Сергеевич

выпуск 19.10.2026 № 53e4f7ddae · стр. 13 из 160

График закупок и работ. Лист 3 из 3

Что заказывать и когда не раньше чего: относительный порядок без дат; срок поставки — из данных или «уточняется у поставщика»

Работы: порядок и что не даёт начать (продолжение)

№	Работа (стадия технологической последовательности)	После	Что должно быть к началу: условия и закупки	Не начинать, пока открыто в реестре
Р-11	Окраска стен, потолков, откосов (стадия 13)	Р-10	до начала: шпаклёвка отшлифована и огрунтована; выкрасы утверждены, колеровка одной партией	
Р-12	Чистовые полы: инженерная доска (стадия 14)	Р-9, Р-11	до начала: влажность основания в норме, мокрые работы закончены; доска выбрана и привезена Закупки к началу: З-7 (доска и плинтус)	
Р-13	Полотна межкомнатных дверей, плинтусы, пороги (стадия 15)	Р-11, Р-12	до начала: чистовой пол уложен; полотна скрытых дверей — после чистовой отделки стен	
Р-14	Чистовая электрика и сантехника: механизмы, светильники, смесители, приборы (стадия 16)	Р-11, Р-13	до начала: отделка готова; механизмы, светильники и приборы выбраны и привезены	
Р-15	Кухня, встроенная и корпусная мебель, бытовая техника (стадия 17)	Р-13, Р-14	до начала: чистовая сантехника и электрика подведены к местам мебели; замер кухни снят по готовым стенам (после штукатурки или плитки, до чистового пола) Закупки к началу: З-2 (кухонный гарнитур), З-3 (техника кухни), З-8 (мебель по замеру)	К-1: Бриф задаёт 11 помещений с габаритами и этажами, но не их взаимное расположение, контур дома и толщины стен: раскладка этажей, контур 9600 × 8000 и перегородки подобраны проектировщиком под габариты брифа.
Р-16	Сдача: осмотр по чек-листу, дефектная ведомость, устранение замечаний (стадия 18)	Р-14, Р-15	до начала: всё смонтировано; акты скрытых работ подписаны	

Примечания

1. Порядок работ — стадии технологической последовательности из 16 позиций, присутствующих в этом проекте (по строкам ведомости объёмов); остальные стадии таблицы knowledge/remont-tehnologiya.md в проекте не встречаются. Длительности работ не печатаются: их нет ни в данных, ни в нормах для этого объекта.
2. Типовые сроки — ориентир практики, не срок поставщика: скрытые двери — короб около 10 дн., полотно под покраску до 3 нед., шпон 4–5 нед., в среднем около 30 дн. (knowledge/workers/foreman.md, п. 2.4 (profil-doors)); кухня и корпусная мебель — 4–8 недель от замера (knowledge/remont-tehnologiya.md, разд. 2; knowledge/workers/foreman.md, п. 2.4). Заказ по ориентиру не назначается: срок получают у поставщика (вопрос реестра), после чего заказ планируют «не позднее чем за срок до начала работы».
3. Условия заказа берутся из реестра открытых вопросов и задания на контрольный обмер: позиция заказывается, когда закрыты замер (графа 1) и решение (графа 2). Закрывать их может только факт или решение автора с подписью; снять строку с листа можно только закрыв запись реестра.
4. Заказ по размеру до контрольного обмера не делают: двери, кухня и встроенная мебель зависят от обмера (К-11, К-13); скрытые двери, кроме того, зависят от решения по нише санузла 2 (проём Д-5 в перегородке П-1).
5. Номера листов — по ведомости рабочих чертежей комплекта (лист «Общие данные»).

Допущения и предложения на листе

Основа листа: взаимное расположение помещений, контур дома 9600 × 8000 и раскладка этажей подобраны проектировщиком под габариты помещений брифа; обмер и проект АР — задание (К-1); высота потолка 2900 мм — по брифу, не замерена; перекрытие 330 мм и отметка 2-го этажа +3,230 приняты; проект КР — задание (К-2); наружные стены 400 мм, перегородки 120 мм приняты (в брифе толщин нет) (К-1); разрешённая мощность 15 кВт принята по типовым ТУ для частного дома (К-4).
См. лист открытых вопросов (лист 6, записи К-1, К-2, К-4).

Изм.	Кол.уч	Лист	№ док.	Подп.	Дата
Разраб.		Кырлан А.С.			19.10.26
Пров.					
ГИП					
Н. контр.					
Утв.					

ГД-2026-012-АИ

Дом 120 м²

Общая площадь 147,36* м² · * размеры приняты, не замерены (реестр — л. 6, К-1)

Дизайн-проект интерьера

Стадия	Лист	Листов
РП	12	130

График закупок и работ. Лист 3 из 3

М б/м

Кырлан Александр Сергеевич

выпуск 19.10.2026 № 53e4f7ddae · стр. 14 из 160

Обмерный план · 1-й этаж

Существующее положение · размеры в мм · отметки от чистого пола

Экспликация помещений

№	Наименование	Площадь, м²
1	Гостиная-кухня	31,32
2	Холл с лестницей	15,51
3	Кабинет	11,00
4	Санузел гостевой	4,17
5	Прихожая	12,20
	Итого (общая площадь)	**147,36**

Условные обозначения

- существующие стены (сечение)
- окно (рама, остекление)
- проём существующий, без заполнения (откосы)
- стояк: К1 — канализация, В1 — ХВС, Т3 — ГВС
- диагональ помещения — контроль прямоугольности
- (1) номер помещения, площадь м²

Примечания

1. Размеры — в мм по чистым поверхностям стен до отделки (по плану заказчика); площади — в м² по тем же размерам. До начала работ выполнить контрольный обмер.
2. За отметку ±0,000 принят чистый пол, не существующий (блок отметок). Н пот. — высота от чистого пола до плиты перекрытия; Н пот. со знаком «*» — принятая высота, не замер (вопрос К-2).
3. Толщины стен: наружные 400 мм, перегородки 120 мм; отличающиеся толщины и уступы размерами на плане.
4. Несущие стены не определены: до технического заключения все стены считать несущими; проёмы и штробы в них не выполнять.
5. Дверные проёмы показаны без заполнения; высота дверных проёмов 2100 мм; низ окон (подоконник) 500, 900 мм от чистого пола, высота окон 1900, 1500 мм.
6. Диагонали — контрольные размеры; «*» — расчёт по принятому контуру (К-1), при обмере заменить замеренным; расхождение более 5 мм подписать на плане как перекос.
7. Размеры проверить на месте до начала работ; расхождение контрольных промеров ≤ 2 %.

Принято, не определено или спорно

полностью — лист 6

К-1 — Бриф задаёт 11 помещений с габаритами и этажами, но не их взаимное расположение, контур дома и толщины стен: раскладка этажей, контур 9600 × 8000 и перегородки подобраны проектировщиком под габариты брифа

К-3 — Лестница по брифу — из холла 1-го этажа; место, тип (одномаршевая прямая, 17 подъёмов 190 × 250, марш 1000), конструкция и ограждение предложение проектировщика

К-5 — Тип дома, материал и конструкция стен и перекрытия, несущие стены, положение стояков и выпусков канализации в брифе не заданы; проект дома (АР, КР, ВК) не передан

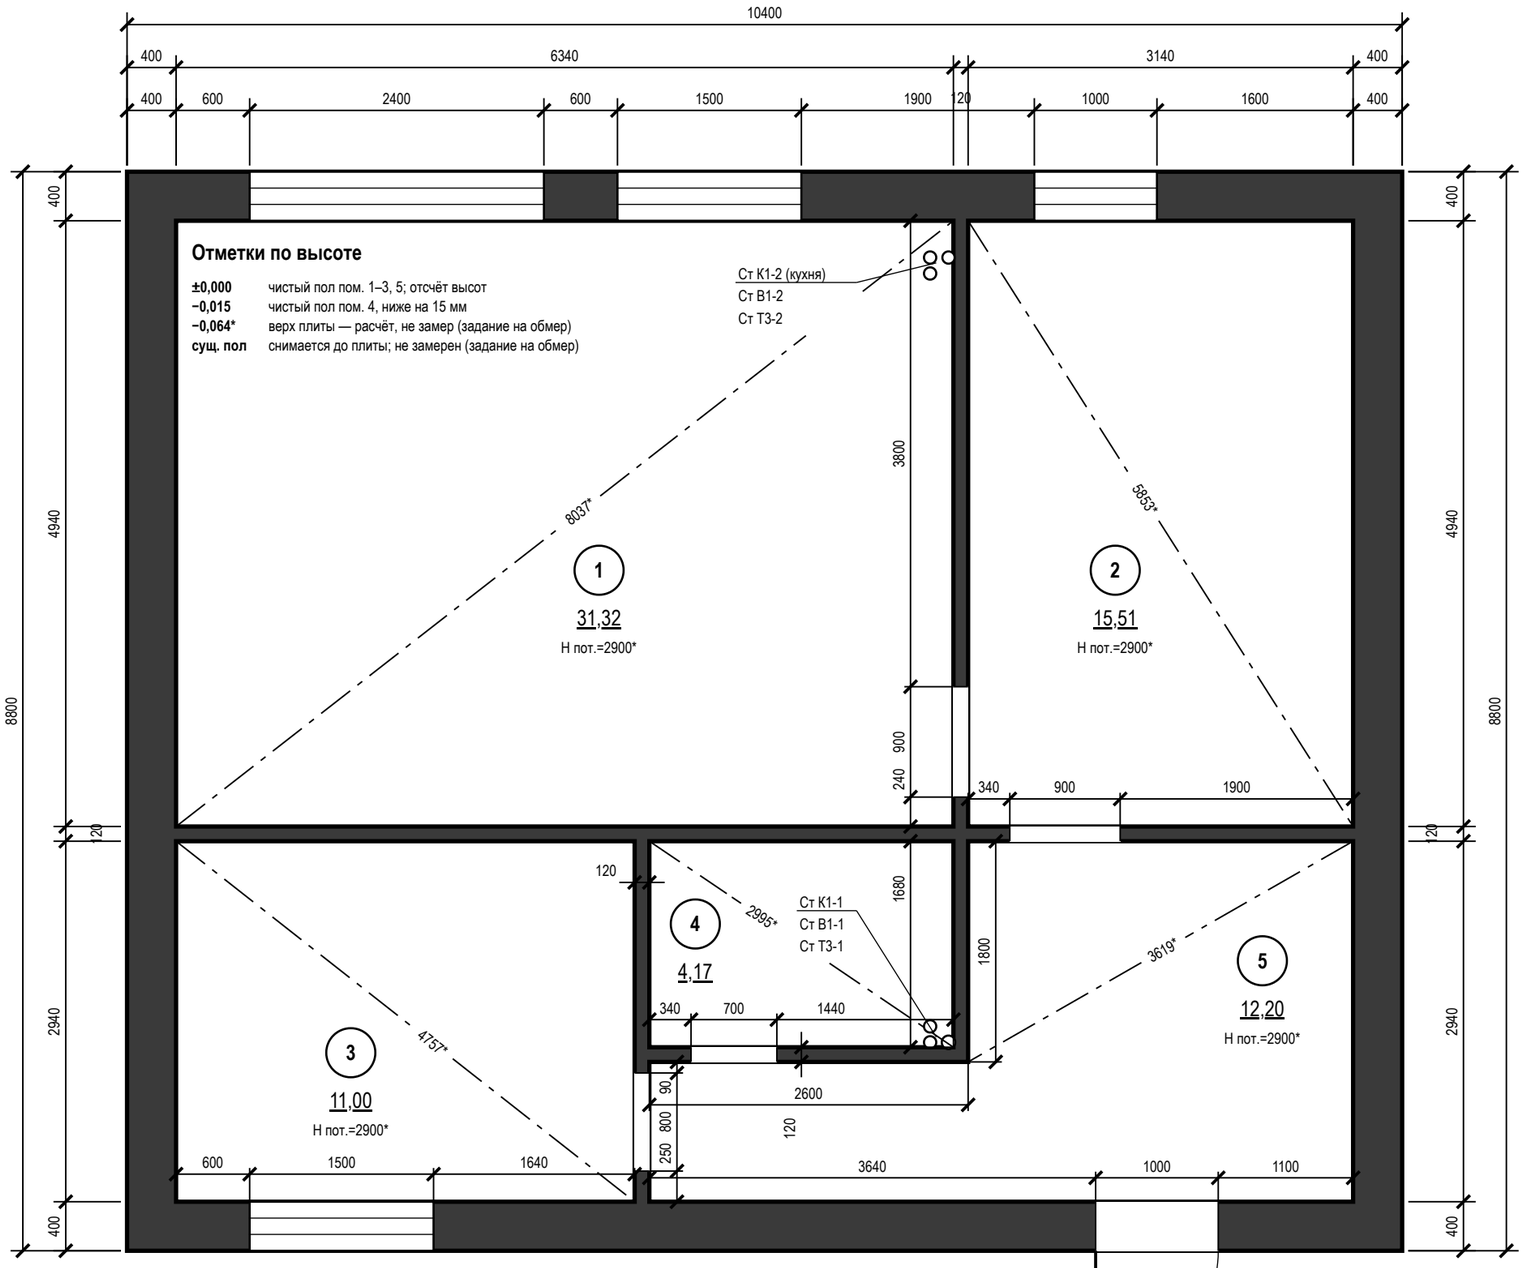

Допущения и предложения на листе

Основа листа: взаимное расположение помещений, контур дома 9600 × 8000 и раскладка этажей подобраны проектировщиком под габариты помещений брифа; обмер и проект АР — задание (К-1); высота потолка 2900 мм — по брифу, не замерена; перекрытие 330 мм и отметка 2-го этажа +3,230 приняты; проект КР — задание (К-2); наружные стены 400 мм, перегородки 120 мм приняты (в брифе толщин нет) (К-1); разрешённая мощность 15 кВт принята по типовым ТУ для частного дома (К-4).

Открытые вопросы и конфликты по листу: К-1–К-3, К-5.

См. лист открытых вопросов (лист 6, записи К-1–К-5).

1000 мм · печать 1:1

Изм.	Кол.уч	Лист	№ док.	Подп.	Дата
Разраб.		Кырлан А.С.			19.10.26
Пров.					
ГИП					
Н. контр.					
Утв.					

ГД-2026-012-АИ

Дом 120 м²

Общая площадь 147,36* м² · * размеры приняты, не замерены (реестр — л. 6, К-1)

Дизайн-проект интерьера

Стадия	Лист	Листов
РП	13	130

Обмерный план · 1-й этаж

М 1:50

Кырлан Александр Сергеевич

выпуск 19.10.2026 № 53e4f7ddae · стр. 15 из 160

Обмерный план · 2-й этаж

Существующее положение · размеры в мм · отметки от чистого пола

ПРЕДВАРИТЕЛЬНО · не для производства работ · открыто пунктов: 6 (реестр — л. 6)

Экспликация помещений

№	Наименование	Площадь, м²
6	Спальня родителей	17,17
7	Детская	12,30
8	Гардеробная	3,82
9	Кладовая	4,66
10	Холл второго этажа	15,51
11	Коридор второго этажа	5,16
12	Детская вторая	9,23
13	Санузел второго этажа	5,31
	Итого (общая площадь)	**147,36**

Условные обозначения

- существующие стены (сечение)
- окно (рама, остекление)
- проём существующий, без заполнения (откосы)
- стояк: К1 — канализация, В1 — ХВС, Т3 — ГВС
- диагональ помещения — контроль прямоугольности
- (1) номер помещения, площадь м²

Примечания

1. Размеры — в мм по чистым поверхностям стен до отделки (по плану заказчика); площади — в м² по тем же размерам. До начала работ выполнить контрольный обмер.
2. За отметку ±0,000 принят чистый пол, не существующий (блок отметок). Н пот. — высота от чистого пола до плиты перекрытия; Н пот. со знаком «*» — принятая высота, не замер (вопрос К-2).
3. Толщины стен: наружные 400 мм, перегородки 120 мм; отличающиеся толщины и уступы размерами на плане.
4. Несущие стены не определены: до технического заключения все стены считать несущими; проёмы и штробы в них не выполнять.
5. Дверные проёмы показаны без заполнения; высота дверных проёмов 2100 мм, проёмов без двери 2100 мм; низ окон (подоконник) 900 мм от чистого пола, высота окон 1500, 1450 мм.
6. Диагонали — контрольные размеры; «*» — расчёт по принятому контуру (К-1), при обмере заменить замеренным; расхождение более 5 мм подписать на плане как перекос.
7. Размеры проверить на месте до начала работ; расхождение контрольных промеров ≤ 2 %.

Отметки по высоте

±0,000	чистый пол пом. 6–12; отсчёт высот
−0,015	чистый пол пом. 13, ниже на 15 мм
−0,064*	верх плиты — расчёт, не замер (задание на обмер)
сущ. пол	снимается до плиты; не замерен (задание на обмер)

Принято, не определено или спорно

полностью — лист 6

К-1 — Бриф задаёт 11 помещений с габаритами и этажами, но не их взаимное расположение, контур дома и толщины стен: раскладка этажей, контур 9600 × 8000 и перегородки подобраны проектировщиком под габариты брифа

К-3 — Лестница по брифу — из холла 1-го этажа; место, тип (одномаршевая прямая, 17 подъёмов 190 × 250, марш 1000), конструкция и ограждение предложение проектировщика

К-5 — Тип дома, материал и конструкция стен и перекрытия, несущие стены, положение стояков и выпусков канализации в брифе не заданы; проект дома (АР, КР, ВК) не передан

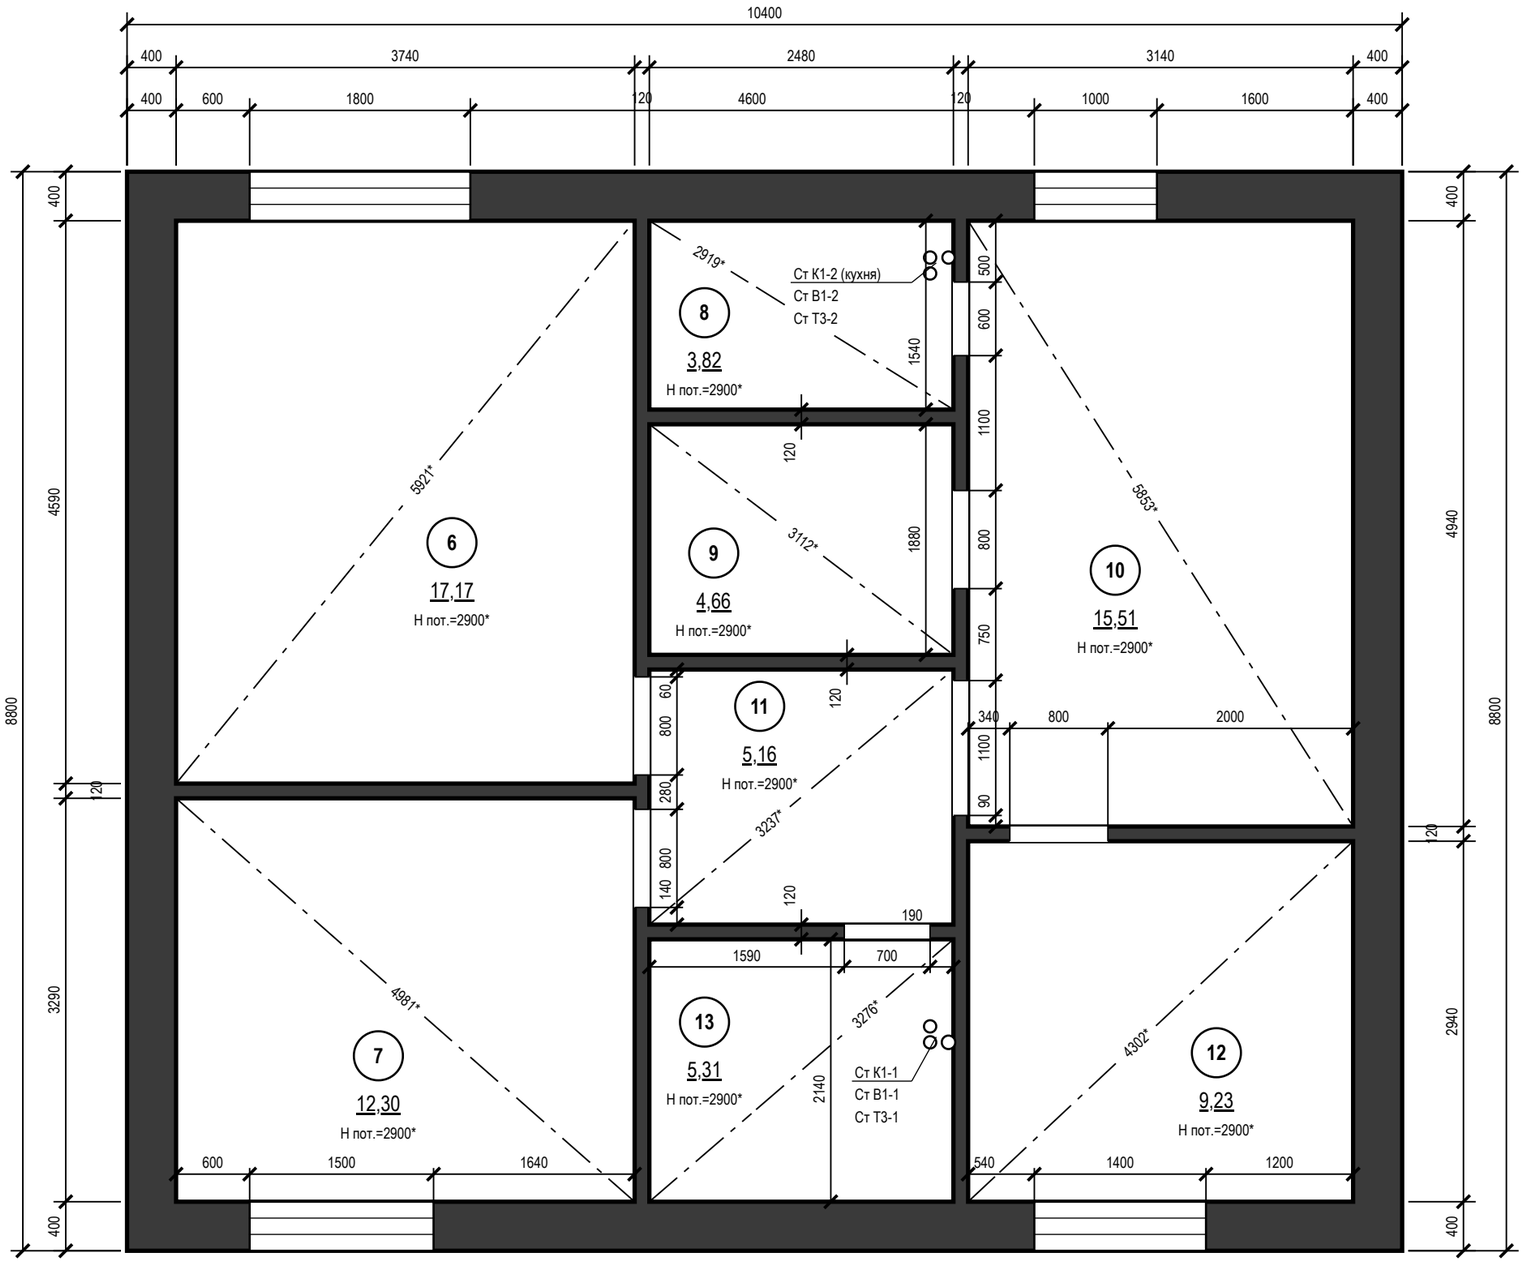

Допущения и предложения на листе

Основа листа: взаимное расположение помещений, контур дома 9600 × 8000 и раскладка этажей подобраны проектировщиком под габариты помещений брифа; обмер и проект АР — задание (К-1); высота потолка 2900 мм — по брифу, не замерена; перекрытие 330 мм и отметка 2-го этажа +3,230 приняты; проект КР — задание (К-2); наружные стены 400 мм, перегородки 120 мм приняты (в брифе толщин нет) (К-1); разрешённая мощность 15 кВт принята по типовым ТУ для частного дома (К-4).

Открытые вопросы и конфликты по листу: К-1–К-3, К-5.

См. лист открытых вопросов (лист 6, записи К-1–К-5).

1000 мм · печать 1:1

Изм.	Кол.уч	Лист	№ док.	Подп.	Дата
Разраб.		Кырлан А.С.			19.10.26
Пров.					
ГИП					
Н. контр.					
Утв.					

ГД-2026-012-АИ

Дом 120 м²

Общая площадь 147,36* м² · * размеры приняты, не замерены (реестр — л. 6, К-1)

Дизайн-проект интерьера

Стадия	Лист	Листов
РП	14	130

Обмерный план · 2-й этаж

М 1:50

Кырлан Александр Сергеевич

выпуск 19.10.2026 № 53e4f7ddae · стр. 16 из 160

План демонтажа и монтажа перегородок · 1-й этаж

Перепланировка не выполняется · существующие стены сохраняются · размеры в мм

ПРЕДВАРИТЕЛЬНО · не для производства работ · открыто пунктов: 6 (реестр — л. 6)

Условные обозначения

- существующие стены — сохраняются;
- несущие не определены — считать несущими
- демонтируемые конструкции — на плане нет
- возводимые перегородки — на плане нет
- проём существующий, без заполнения (откосы)
- (1) номер помещения, площадь м²

Примечания

1. Перепланировка не выполняется: несущие и ненесущие стены, перегородки и плиты перекрытия не демонтируются, новые стены не возводятся; существующие стены и перегородки сохраняются.
2. Дверные блоки — по плану дверей; существующие проёмы не расширяются.
3. Демонтаж существующих покрытий пола, стен и потолка, дверных блоков и сантехприборов (если есть) — до основания; объёмы демонтажа — для справки, по факту на объекте.
4. За отметку ±0,000 принят чистый пол, не существующий (блок отметок). Размеры — в мм по чистовой поверхности стен до отделки.
5. Размеры проверить на месте до начала работ: расхождение с обмером — не более 2 % (иначе — к архитектору).
6. Несущие стены не определены: до технического заключения все стены считать несущими — проёмы, ниши и штробы в них не выполнять.

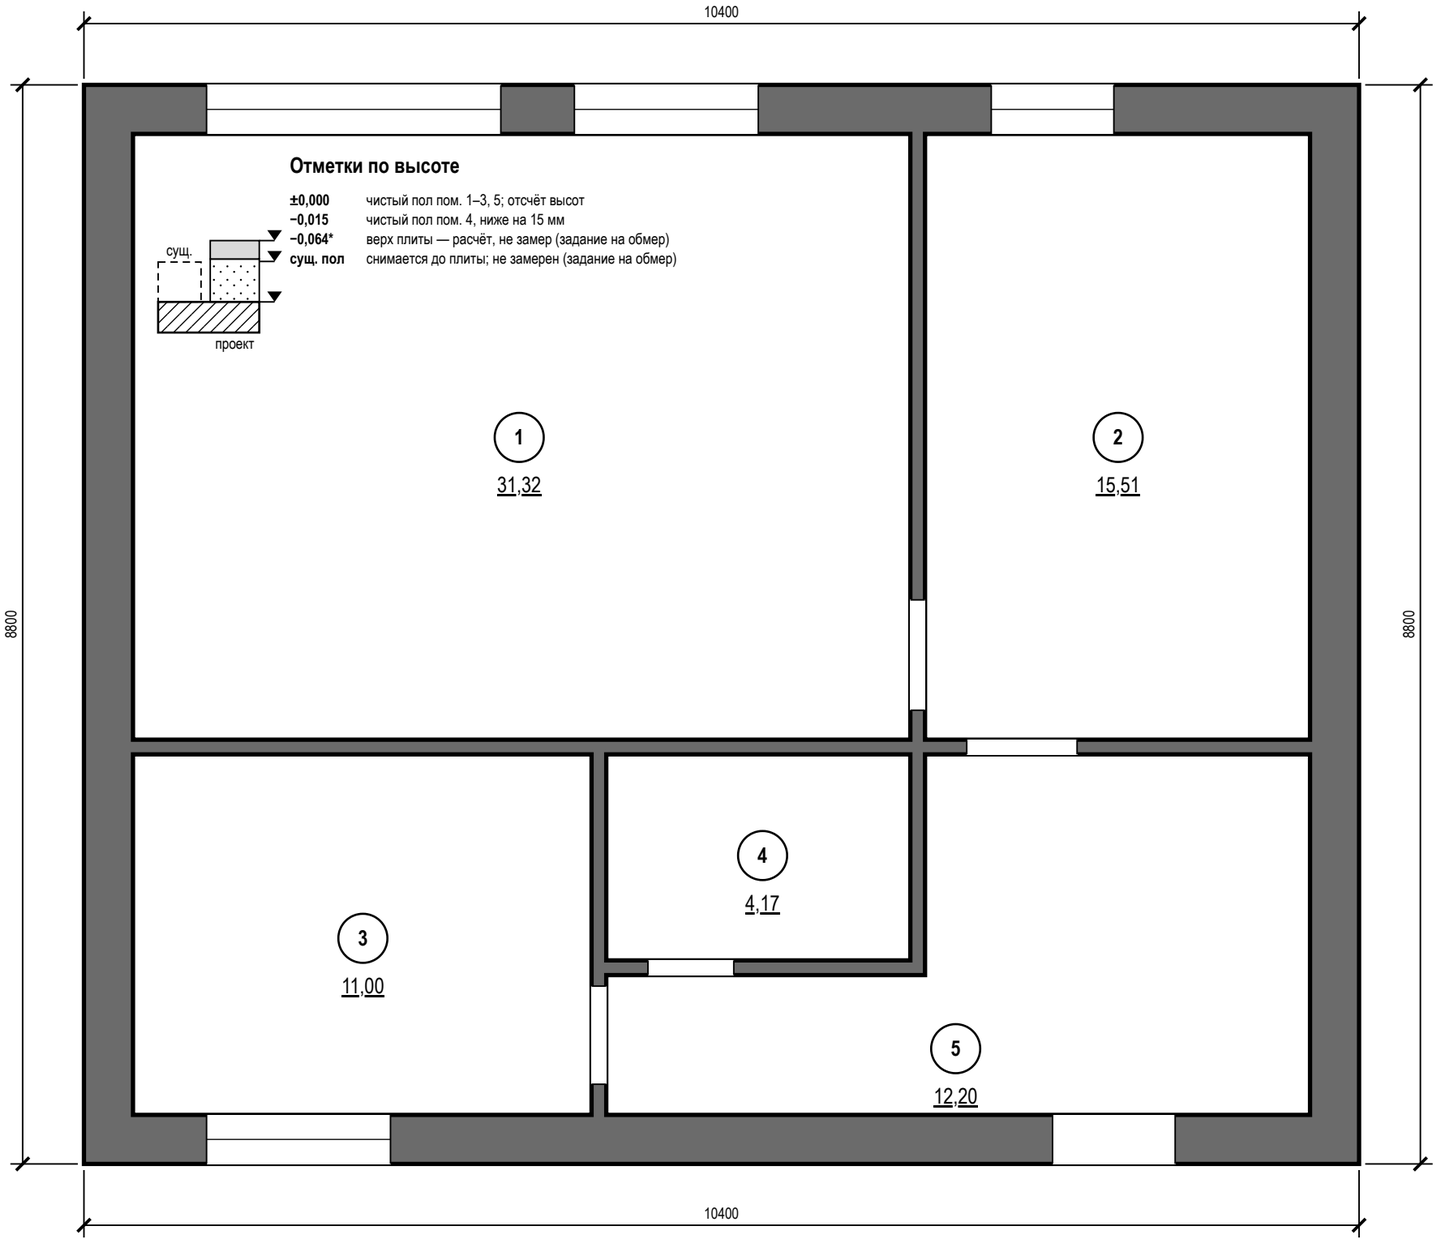

Допущения и предложения на листе

Основа листа: взаимное расположение помещений, контур дома 9600 × 8000 и раскладка этажей подобраны проектировщиком под габариты помещений брифа; обмер и проект АР — задание (К-1); высота потолка 2900 мм — по брифу, не замерена; перекрытие 330 мм и отметка 2-го этажа +3,230 приняты; проект КР — задание (К-2); наружные стены 400 мм, перегородки 120 мм приняты (в брифе толщин нет) (К-1); разрешённая мощность 15 кВт принята по типовым ТУ для частного дома (К-4).

См. лист открытых вопросов (лист 6, записи К-1, К-2, К-4).

1000 мм · печать 1:1

Изм.	Кол.уч	Лист	№ док.	Подп.	Дата
Разраб.		Кырлан А.С.			19.10.26
Пров.					
ГИП					
Н. контр.					
Утв.					

ГД-2026-012-АИ

Дом 120 м²

Общая площадь 147,36* м² · * размеры приняты, не замерены (реестр — л. 6, К-1)

Дизайн-проект интерьера

Стадия	Лист	Листов
РП	15	130

План демонтажа и монтажа перегородок · 1-й этаж

М 1:50

Кырлан Александр Сергеевич

План демонтажа и монтажа перегородок · 2-й этаж

Перепланировка не выполняется · существующие стены сохраняются · размеры в мм

ПРЕДВАРИТЕЛЬНО · не для производства работ · открыто пунктов: 6 (реестр — л. 6)

Условные обозначения

- существующие стены — сохраняются;
- несущие не определены — считать несущими
- демонтируемые конструкции — на плане нет
- возводимые перегородки — на плане нет
- проём существующий, без заполнения (откосы)
- (1) номер помещения, площадь м²

Примечания

1. Перепланировка не выполняется: несущие и ненесущие стены, перегородки и плиты перекрытия не демонтируются, новые стены не возводятся; существующие стены и перегородки сохраняются.
2. Дверные блоки — по плану дверей; существующие проёмы не расширяются.
3. Демонтаж существующих покрытий пола, стен и потолка, дверных блоков и сантехприборов (если есть) — до основания; объёмы демонтажа — для справки, по факту на объекте.
4. За отметку ±0,000 принят чистый пол, не существующий (блок отметок). Размеры — в мм по чистовой поверхности стен до отделки.
5. Размеры проверить на месте до начала работ: расхождение с обмером — не более 2 % (иначе — к архитектору).
6. Несущие стены не определены: до технического заключения все стены считать несущими — проёмы, ниши и штробы в них не выполнять.

Отметки по высоте

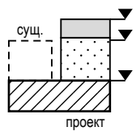

±0,000	чистый пол пом. 6–12; отсчёт высот
−0,015	чистый пол пом. 13, ниже на 15 мм
−0,064*	верх плиты — расчёт, не замер (задание на обмер)
сущ. пол	снимается до плиты; не замерен (задание на обмер)

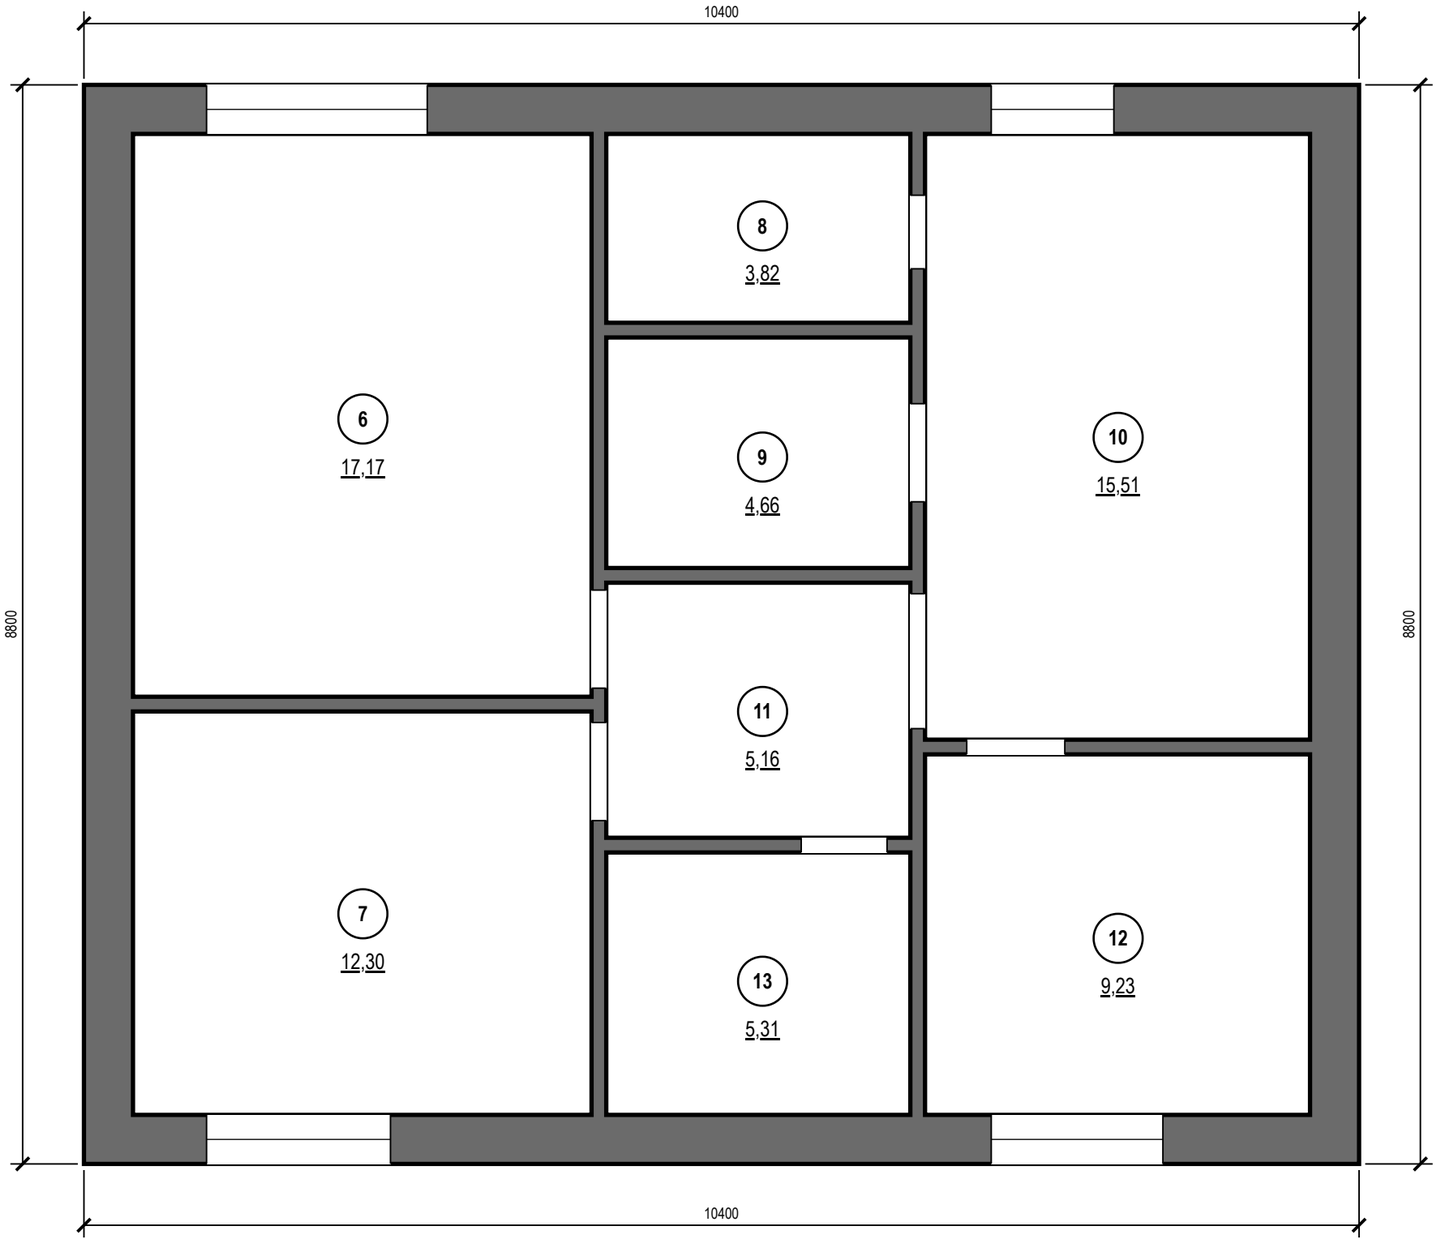

Допущения и предложения на листе

Основа листа: взаимное расположение помещений, контур дома 9600 × 8000 и раскладка этажей подобраны проектировщиком под габариты помещений брифа; обмер и проект АР — задание (К-1); высота потолка 2900 мм — по брифу, не замерена; перекрытие 330 мм и отметка 2-го этажа +3,230 приняты; проект КР — задание (К-2); наружные стены 400 мм, перегородки 120 мм приняты (в брифе толщин нет) (К-1); разрешённая мощность 15 кВт принята по типовым ТУ для частного дома (К-4).

См. лист открытых вопросов (лист 6, записи К-1, К-2, К-4).

1000 мм · печать 1:1

Изм.	Кол.уч	Лист	№ док.	Подп.	Дата
Разраб.		Кырлан А.С.			19.10.26
Пров.					
ГИП					
Н. контр.					
Утв.					

ГД-2026-012-АИ

Дом 120 м²

Общая площадь 147,36* м² · * размеры приняты, не замерены (реестр — л. 6, К-1)

Дизайн-проект интерьера

Стадия	Лист	Листов
РП	16	130

План демонтажа и монтажа перегородок · 2-й этаж

М 1:50

Кырлан Александр Сергеевич

выпуск 19.10.2026 № 53e4f7ddae · стр. 18 из 160

План дверей и ведомость заполнения проёмов · 1-й этаж

Проёмы, марки заполнения, привязки · размеры в мм

ПРЕДВАРИТЕЛЬНО · не для производства работ · открыто пунктов: 6 (реестр — л. 6)

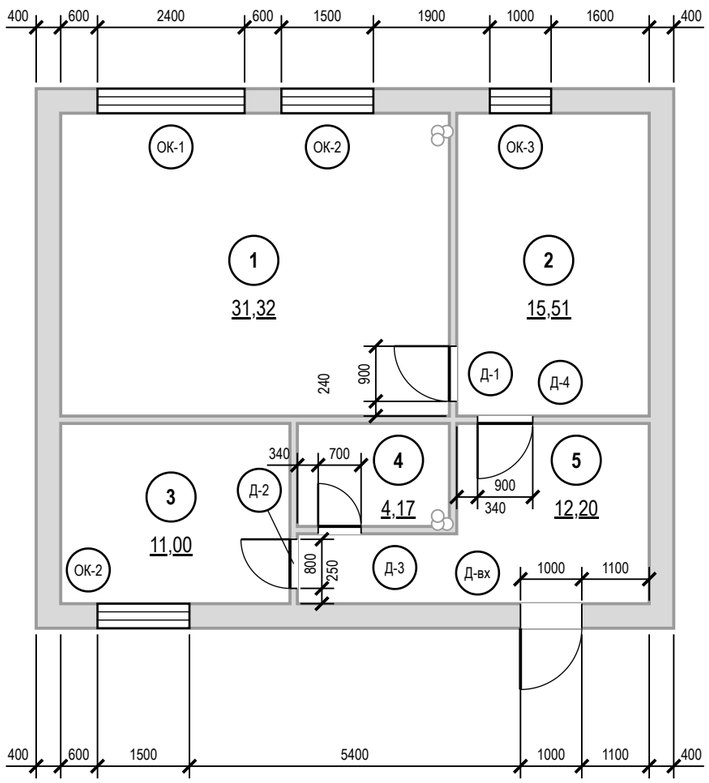

Ведомость заполнения проёмов

Марка	Наименование, обозначение	Проём ш×в, мм	Кол.	Откр.	Отделка полотна	Фурнитура	Прим.
Д-вх	Блок дверной входной, ГОСТ 31173-2016	1000×2100	1	Л	в комплекте блока	в комплекте блока (замки, глазок)	наружу
Д-1	Дверь скрытого монтажа, ТУ изготовителя	900×2100	1	Л	окраска G503 с двух сторон	скрытые петли 3D, магнитный замок	
Д-2	Дверь скрытого монтажа, ТУ изготовителя	800×2100	1	Л	окраска G503 с двух сторон	скрытые петли 3D, магнитный замок	
Д-3	Дверь скрытого монтажа, ТУ изготовителя	700×2100	1	П	в тон облицовки — пом. 4, G503 — пом. 5	скрытые петли 3D, магнитный замок, фиксатор WC	порог 15
Д-4	Дверь скрытого монтажа, ТУ изготовителя	900×2100	1	Л	окраска G503 с двух сторон	скрытые петли 3D, магнитный замок	
ОК-1	Блок оконный, ГОСТ 23166-2021; стекло — триплекс	2400×1900	1				низ 500
ОК-2	Блок оконный, ГОСТ 23166-2021	1500×1500	2				низ 900
ОК-3	Блок оконный, ГОСТ 23166-2021	1000×1500	1				низ 900

Условные обозначения

- стены (подложка обмера)
- дверь распашная, дуга открывания
- дверь скрытого монтажа
- дверь входная (полотно толще)
- оконный блок
- Д — марка типа (Д-N, ОК-N)
- 1 — номер помещения, площадь м²

Примечания

1. Размеры проёмов и привязки — в миллиметрах от чистых граней стен до отделки; привязка — от угла того помещения, со стороны которого стоит размер. Размер в ведомости — ширина × высота проёма от чистого пола 0,000. Откос от угла помещения до проёма с коробкой — не менее 50 мм.
2. Марки в кружках — типы заполнения проёмов (ГОСТ 21.501-2018, п. 5.3.2); одна марка — один типоразмер; количество сверено с планом.
3. Открывание: Л — петли слева, П — справа, если смотреть со стороны, куда открывается полотно (на себя).
4. Остекление окон: ОК-1 (пом. 1) — триплекс. Тип стекла указать при заказе оконных блоков; замена на другое стекло — только по согласованию с автором проекта.
5. ОК-1: низ остекления 500 мм — ниже 900 мм от чистого пола, поэтому окно заказывать с безопасным стеклом (триплекс); ограждение проёма в проекте не задано (СП 54.13330.2022, п. 6.4.9; ГОСТ Р 56926).
6. Скрытые двери (Д-1…Д-4): проём замерить в чистоте; блок заказать до штукатурки (≈ 30 дн.), короб ставить до штукатурки; полотно навесить после чистовой отделки, красить в цвет стен. Порядок практика монтажа, изготовитель подтверждает.
7. Размер в ведомости — проёма: полотно скрытой двери уже проёма на коробку и зазор 10–15 мм (модель не выбрана); Д-1…Д-4 — существующие проёмы, до техзаключения не расширять.
8. Д-вх: дуга наружу — по плану заказчика, не проверено; блок оставить или заменить — не решено.
9. Привязка проёма к углу помещения меньше 1 мм на листе, размер на плане не показан: Д-2 — 90 мм.

Допущения и предложения на листе

Основа листа: взаимное расположение помещений, контур дома 9600 × 8000 и раскладка этажей подобраны проектировщиком под габариты помещений брифа; обмер и проект АР — задание (К-1); высота потолка 2900 мм — по брифу, не замерена; перекрытие 330 мм и отметка 2-го этажа +3,230 приняты; проект КР — задание (К-2); наружные стены 400 мм, перегородки 120 мм приняты (в брифе толщин нет) (К-1); разрешённая мощность 15 кВт принята по типовым ТУ для частного дома (К-4).
См. лист открытых вопросов (лист 6, записи К-1, К-2, К-4).

1000 мм · печать 1:1

Изм.	Кол.уч	Лист	№ док.	Подп.	Дата			
Разраб.		Кырлан А.С.			19.10.26	**ГД-2026-012-АИ**		
Пров.						Дом 120 м²		
ГИП						Общая площадь 147,36* м² · * размеры приняты, не замерены (реестр — л. 6, К-1)		
						Дизайн-проект интерьера	Стадия: РП	Лист: 17 / Листов: 130
Н. контр.						**План дверей и ведомость заполнения проёмов · 1-й этаж** М 1:100	**Кырлан Александр Сергеевич**	
Утв.								

выпуск 19.10.2026 № 53e47ddae · стр. 19 из 160

План дверей и ведомость заполнения проёмов · 2-й этаж

Проёмы, марки заполнения, привязки · размеры в мм

ПРЕДВАРИТЕЛЬНО · не для производства работ · открыто пунктов: 6 (реестр — л. 6)

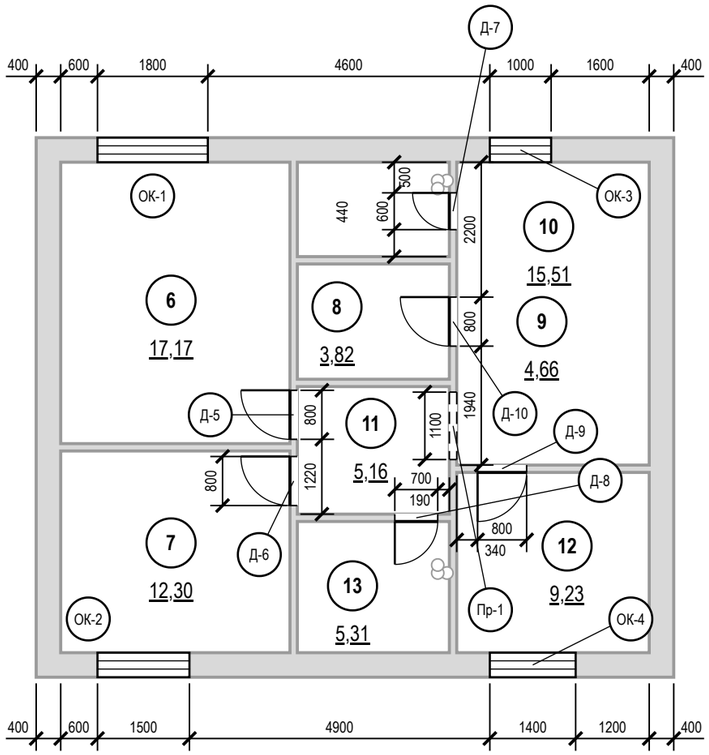

Ведомость заполнения проёмов

Марка	Наименование, обозначение	Проём ш×в, мм	Кол.	Откр.	Отделка полотна	Фурнитура	Прим.
Д-5	Дверь скрытого монтажа, ТУ изготовителя	800×2100	1	Л	окраска G503 с двух сторон	скрытые петли 3D, магнитный замок	
Д-6	Дверь скрытого монтажа, ТУ изготовителя	800×2100	1	Л	окраска G503 с двух сторон	скрытые петли 3D, магнитный замок	
Д-7	Дверь скрытого монтажа, ТУ изготовителя	600×2100	1	Л	No. 222 — пом. 8, G503 — пом. 10	скрытые петли 3D, магнитный замок	
Д-8	Дверь скрытого монтажа, ТУ изготовителя	700×2100	1	Л	в тон облицовки — пом. 13, G503 — пом. 11	скрытые петли 3D, магнитный замок, фиксатор WC	порог 15
Д-9	Дверь скрытого монтажа, ТУ изготовителя	800×2100	1	Л	окраска G503 с двух сторон	скрытые петли 3D, магнитный замок	
Д-10	Дверь скрытого монтажа, ТУ изготовителя	800×2100	1	Л	S 0502-Y — пом. 9, G503 пом. 10	скрытые петли 3D, магнитный замок	
Пр-1	Портал без заполнения	1100×2100	1				б/п
ОК-1	Блок оконный, ГОСТ 23166-2021	1800×1500	1				низ 900
ОК-2	Блок оконный, ГОСТ 23166-2021	1500×1450	1				низ 900
ОК-3	Блок оконный, ГОСТ 23166-2021	1000×1500	1				низ 900
ОК-4	Блок оконный, ГОСТ 23166-2021	1400×1450	1				низ 900

Условные обозначения

- стены (подложка обмера)
- дверь распашная, дуга открывания
- дверь скрытого монтажа
- портал (штрих — перемычка)
- оконный блок
- Д — марка типа (Д-N, ПР-N, ОК-N)
- 1 — номер помещения, площадь м²

Примечания

1. Размеры проёмов и привязки — в миллиметрах от чистых граней стен до отделки; привязка — от угла того помещения, со стороны которого стоит размер. Размер в ведомости — ширина × высота проёма от чистого пола 0,000. Откос от угла помещения до проёма с коробкой — не менее 50 мм.
2. Марки в кружках — типы заполнения проёмов (ГОСТ 21.501-2018, п. 5.3.2); одна марка — один типоразмер; количество сверено с планом.
3. Открывание: Л — петли слева, П — справа, если смотреть со стороны, куда открывается полотно (на себя).
4. Скрытые двери (Д-5…Д-10): проём замерить в чистоте; блок заказать до штукатурки (≈ 30 дн.), короб ставить до штукатурки; полотно навесить после чистовой отделки, красить в цвет стен. Порядок практика монтажа, изготовитель подтверждает.
5. Размер в ведомости — проёма: полотно скрытой двери уже проёма на коробку и зазор 10–15 мм (модель не выбрана); Д-5…Д-10 — существующие проёмы, до техзаключения не расширять.
6. Привязка проёма к углу помещения меньше 1 мм на листе, размер на плане не показан: Д-5 — 60 мм; Д-6 — 90 мм; Пр-1 — 90 мм.

Допущения и предложения на листе

Основа листа: взаимное расположение помещений, контур дома 9600 × 8000 и раскладка этажей подобраны проектировщиком под габариты помещений брифа; обмер и проект АР — задание (К-1); высота потолка 2900 мм — по брифу, не замерена; перекрытие 330 мм и отметка 2-го этажа +3,230 приняты; проект КР — задание (К-2); наружные стены 400 мм, перегородки 120 мм приняты (в брифе толщин нет) (К-1); разрешённая мощность 15 кВт принята по типовым ТУ для частного дома (К-4).
См. лист открытых вопросов (лист 6, записи К-1, К-2, К-4).

1000 мм · печать 1:1

Изм.	Кол.уч	Лист	№ док.	Подп.	Дата
Разраб.		Кырлан А.С.			19.10.26
Пров.					
ГИП					
Н. контр.					
Утв.					

ГД-2026-012-АИ

Дом 120 м²

Общая площадь 147,36* м² · * размеры приняты, не замерены (реестр — л. 6, К-1)

Дизайн-проект интерьера

Стадия	Лист	Листов
РП	18	130

План дверей и ведомость заполнения проёмов · 2-й этаж

М 1:100

Кырлан Александр Сергеевич

выпуск 19.10.2026 № 53e4f7ddae · стр. 20 из 160

Лестница Л-1*

План марша, разрез 1-1, узел крепления стойки ограждения, спецификация · отметки от ±0,000 (чистый пол этажа 1) · размеры в мм

ПРЕДВАРИТЕЛЬНО · не для производства работ · открыто пунктов: 6 (реестр — л. 6)

План марша Л-1* (М 1:50) · 2. Холл с лестницей

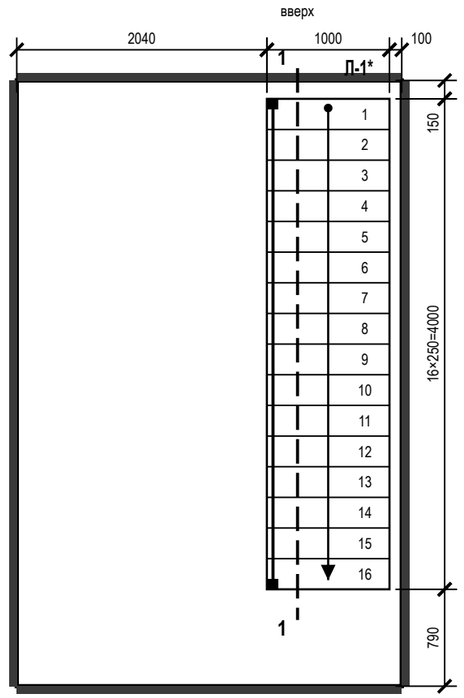

Разрез 1-1 (М 1:50)

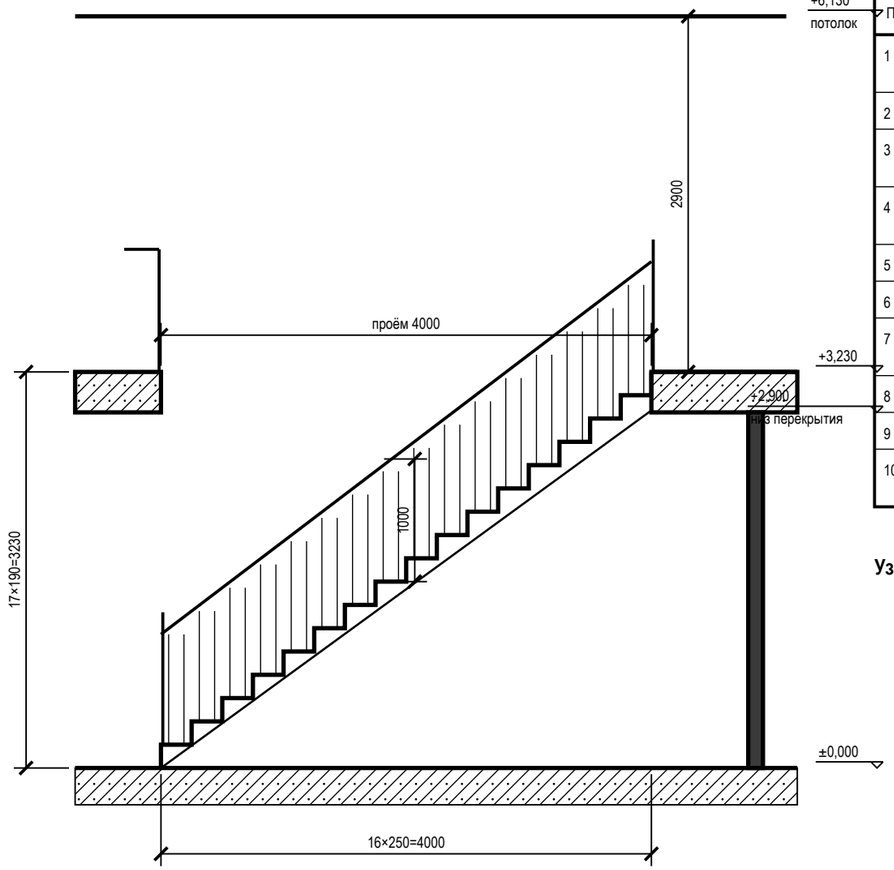

Спецификация элементов лестницы Л-1*

Поз.	Наименование	Кол.	Материал, сечение	Примечание
1	Ступень (проступь)	16	дуб табак, 40 мм	1000×250, толщина по изделию
2	Подступенок	17	дуб табак	высота 190
3	Косоур	2	косоуры стальные, тёплый графит	несущие марша
4	Столб ограждения марша	2	дуб табак, стойки — графит	по концам марша, стороны Г
5	Балясина	45	дуб табак, стойки — графит	шаг 110, просвет 80
6	Поручень марша	1	Ø40	L ≈ 5,02 м, h 900
7	Столб ограждения проёма	2	дуб табак, стойки — графит	углы проёма, стороны Г
8	Балясина ограждения проёма	36	дуб табак, стойки — графит	шаг 110
9	Поручень ограждения проёма	1	Ø40	L ≈ 4,00 м, h 1000
10	Крепёж ограждения	1	комплект по изделию	нагрузка на поручень 0,5 кН/м

Узел 1. Крепление стойки ограждения (М 1:5)

Зазор заполнения до ступени 100 (ГОСТ 25772, прил. А); узел типовой, уточнить по изделию

Примечания

1. Лестница Л-1*: 17 подъёмов × 190 мм = 3230 мм (отм. ±0,000 … +3,230), проступь 250 мм, ширина марша 1000 мм; уклон 37,2°, шаг 2h + b = 630 мм (удобно 600–640 — практика).
2. Ограждение марша со стороны Г: балясины, просвет между элементами 80 мм (не больше 150 — ГОСТ 25772-2025, табл. 3, тип МВ); высота 1000 мм, поручень с одной стороны на 900 мм по линии носков (не менее 900 — СП 55.13330.2016, п. 8.3; СП 59.13330.2020, п. 6.2.11).
3. Проём в перекрытии 1000×4000 мм на этаже 2 ограждён со сторон Г высотой 1000 мм, непрерывно, с поручнем (СП 55.13330.2016, п. 8.3); нагрузка на поручень 0,5 кН/м (СП 20.13330.2016, п. 8.2.6).
4. Просвет над линией носков — не менее 2900 мм (ступень 17, под потолком мансарды); рекомендуется не менее 2000, путь эвакуации — 2200 (СП 55.13330.2016, п. 7.4).
5. Все подступенки одной высоты (СП 55.13330.2016, п. 8.2). Размеры по месту уточнить после обмера: разность отметок чистых полов замерить до заказа изделия.
6. Узел 1 — типовое решение крепления стойки к косоуру; крепёж, сечения и материал — по проекту изделия изготовителя лестницы.

Допущения и предложения на листе

Основа листа: взаимное расположение помещений, контур дома 9600 × 8000 и раскладка этажей подобраны проектировщиком под габариты помещений брифа; обмер и проект АР — задание (К-1); высота потолка 2900 мм — по брифу, не замерена; перекрытие 330 мм и отметка 2-го этажа +3,230 приняты; проект КР — задание (К-2); наружные стены 400 мм, перегородки 120 мм приняты (в брифе толщин нет) (К-1); разрешённая мощность 15 кВт принята по типовым ТУ для частного дома (К-4).

Знак «*» — принято, не замерено и не подтверждено (замерить на объекте): К-3: Л-1 — место, тип и размеры лестницы брифом не заданы (только «лестница из холла 1-го этажа»): одномаршевая 17 × 190 × 250 вдоль стены Б холла — предложение проектировщика; конструкция и расчёт — проект КР.

См. лист открытых вопросов (лист 6, записи К-1–К-4).

1000 мм · печать 1:1

Изм.	Кол.уч	Лист	№ док.	Подп.	Дата
Разраб.		Кырлан А.С.			19.10.26
Пров.					
ГИП					
Н. контр.					
Утв.					

ГД-2026-012-АИ

Дом 120 м²

Общая площадь 147,36* м² · * размеры приняты, не замерены (реестр — л. 6, К-1)

Дизайн-проект интерьера	Стадия	Лист	Листов
	РП	19	130

Лестница Л-1

М 1:50

Кырлан Александр Сергеевич

выпуск 19.10.2026 № 53e4f7ddae · стр. 21 из 160

Концепция интерьера · 1-й этаж

Средиземноморский · схема комплементарная · 60/30/10 · материалы, образы и зонирование

ПРЕДВАРИТЕЛЬНО · не для производства работ · открыто пунктов: 6 (реестр — л. 6)

Идея

Стиль — средиземноморский: солнце и воздух, морская свежесть, неторопливость, тёплая простота, жизнь на террасе. Средиземноморский 60 % + скандинавский (scandinavian.json) 40 %: дом у соснового бора, светлый и солнечный. Стены — кремовый белый Calla G503 и известковый Wimborne White No. 239, потолки — Loft White No. 222; второй план светлый песок S 1010-Y20R, морская лазурь Lulworth Blue No. 89, серо-оливковая листва Treron No. 292; акценты эгейский синий S 3050-R80B, охра India Yellow No. 66, олива S 5020-G90Y. По брифу: дерево — дуб табак (мебель, лестница), фурнитура и светильники — латунь, рамы и металл — тёплый графит; свет тёплый 2700–3000 K, фасады матовые. Цветовая схема — комплементарная, пропорция 60/30/10: база на стенах и потолках, вторичный цвет — в текстиле и мягкой мебели, акцент — точечно.

Мудборд: материалы и фактуры

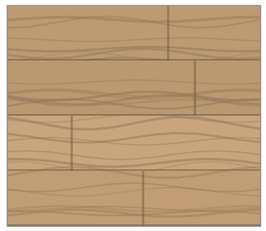

1167-4250
пол

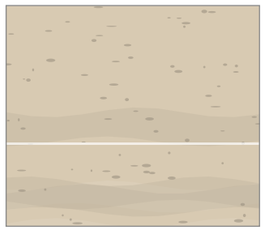

Керамогранит под травертин
фартук

 

Loft White · Little Greene No. 222
потолок

Calla · Tikkurila G503
стены, плинтус

Эгейский синий · NCS S 3050-R80B
акцент (стена А)

Олива · NCS S 5020-G90Y
акцент (стена А)

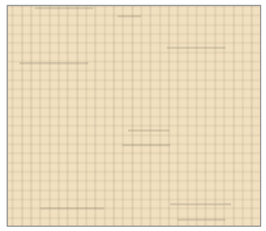

Лён, NCS S 1010-Y20R
портьеры-волна

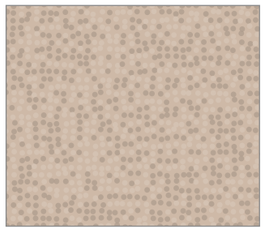

Шерсть, Tikkurila X463
ковёр в зоне отдыха, плед на диван

Бархат, NCS S 3050-R80B
подушки на диван

Палитра 60/30/10

60 % база — Tikkurila G503 Calla, LRV 89; Farrow & Ball No. 239 Wimborne White — белый с каплей тёплой охры, LRV 89; Little Greene No. 222 Loft White, LRV 92

30 % вторичный — NCS S 1010-Y20R Светлый песок / известняк, LRV 75; Farrow & Ball No. 89 Lulworth Blue — светлая морская лазурь, LRV 45; Farrow & Ball No. 292 Treron — серо-оливковая листва, LRV 15

10 % акцент — NCS S 3050-R80B Эгейский синий, LRV 13; Farrow & Ball No. 66 India Yellow — охра / горчица итальянских фасадов, LRV 36; NCS S 5020-G90Y Олива, LRV 20

Допущения и предложения на листе

Основа листа: взаимное расположение помещений, контур дома 9600 × 8000 и раскладка этажей подобраны проектировщиком под габариты помещений брифа; обмер и проект АР — задание (К-1); высота потолка 2900 мм — по брифу, не замерена; перекрытие 330 мм и отметка 2-го этажа +3,230 приняты; проект КР — задание (К-2); наружные стены 400 мм, перегородки 120 мм приняты (в брифе толщин нет) (К-1); разрешённая мощность 15 кВт принята по типовым ТУ для частного дома (К-4).

Примечания

См. лист открытых вопросов (лист 6, записи К-1, К-2, К-4).

1. Коды цвета — по веерам производителей (колерная карта, лист 62); перед закупкой краски — выкрас на стене объекта под дневным светом и лампами проекта.
2. Материалы — по ведомости отделки (лист 60); мебель, текстиль и декор — по спецификации (лист 24). Образцы доски, керамогранита и тканей утвердить до заказа.
3. Фактуры на листе условные, цвет передан по HEX-значениям производителей: при печати возможны отклонения, решение — только по физическому образцу.

Функциональное зонирование (М 1:200)

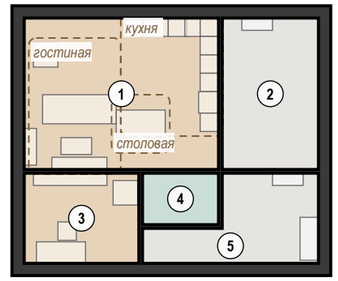

- дневная зона: гостиная, кухня, столовая
- мокрая зона: санузлы
- вход и коммуникации
- функциональная зона в помещении
- (1) номер помещения (лист 22)

Образы помещений

1. Гостиная-кухня — 31,32 м²

стены Tikkurila G503; акцент S 3050-R80B на стене А
пол — 1167-4250
текстиль: портьеры S 1010-Y20R, тюль No. 222, римская штора X463, ковёр в зоне отдыха X463
декор: картина над креслом, растение, ваза

3. Кабинет — 11,00 м²

стены Tikkurila G503; акцент S 5020-G90Y на стене А
пол — 1167-4250
текстиль: портьеры S 1010-Y20R, тюль No. 222, ковёр X463
декор: картина над креслом

5. Прихожая — 12,20 м²

стены Tikkurila G503
пол — A8UZ
декор: зеркало, Замиокулькас в кашпо
свет 3000/2700 K

2. Холл с лестницей — 15,51 м²

стены Tikkurila G503
пол — 1167-4250
декор: Сансевиерия в кашпо
свет 3000 K

4. Санузел гостевой — 4,17 м²

стены Atlas Concorde A8UZ
пол — A8UZ
декор: зеркало над умывальником
свет 3000 K

Материалы и отделка

1167-4250
пол — пом. 1, 2, 3

Керамогранит под травертин
матовый; 1200×600
фартук — пом. 1

A8UZ
пол, стены — пом. 4, 5

Tikkurila G503 Calla, LRV 89
Farrow & Ball Modern Emulsion, матовая
стены, плинтус — пом. 1, 2, 3, 5

Little Greene No. 222 Loft White, LRV 92
Tikkurila Anti-Reflex 2, глубокоматовая
потолок — пом. 1, 2, 3, 4, 5

NCS S 3050-R80B Эгейский синий, LRV 13
акцентная стена
акцент (стена А) — пом. 1

NCS S 5020-G90Y Олива, LRV 20
акцентная стена
акцент (стена А) — пом. 3

Текстиль и металл

Лён, NCS S 1010-Y20R
портьеры-волна

Лён, Tikkurila X463
римская штора

Букле, NCS S 1010-Y20R
подушки на диван, подушки декоративные на кровать

Бархат, NCS S 5020-G90Y
подушки на кровать

Чёрный матовый металл
зеркало

Вуаль, Little Greene No. 222
тюль

Шерсть, Tikkurila X463
ковёр в зоне отдыха, плед на диван

Бархат, NCS S 3050-R80B
подушки на диван

Шерсть, NCS S 5020-G90Y
плед на кровать

Чего избегаем

1) Глянец и пластик под камень
2) Холодный белый 6500 K и LED-ленты холодного оттенка
3) Ракушки, якоря, штурвалы толпой — это морской китч, не средиземноморье
4) Ярко-синие стены в северной комнате без тёплой основы
5) Глянцевая кафельная плитка под котто
6) Тяжёлые портьеры и ламбрекены

Изм.	Кол.уч	Лист	№ док.	Подп.	Дата
Разраб.		Кырлан А.С.			19.10.26
Пров.					
ГИП					
Н. контр.					
Утв.					

ГД-2026-012-АИ

Дом 120 м²

Общая площадь 147,36* м² · * размеры приняты, не замерены (реестр — л. 6, К-1)

Дизайн-проект интерьера

Стадия	Лист	Листов
РП	20	130

Концепция интерьера · 1-й этаж

М б/м

Кырлан Александр Сергеевич

выпуск 19.10.2026 № 53e4f7ddae · стр. 22 из 160

Концепция интерьера · 2-й этаж

Средиземноморский · схема комплементарная · 60/30/10 · материалы, образы и зонирование

ПРЕДВАРИТЕЛЬНО · не для производства работ · открыто пунктов: 6 (реестр — л. 6)

Идея

Стиль — средиземноморский: солнце и воздух, морская свежесть, неторопливость, тёплая простота, жизнь на террасе. Средиземноморский 60 % + скандинавский (scandinavian.json) 40 %: дом у соснового бора, светлый и солнечный. Стены — кремовый белый Calla G503 и известковый Wimborne White No. 239, потолки — Loft White No. 222; второй план светлый песок S 1010-Y20R, морская лазурь Lulworth Blue No. 89, серо-оливковая листва Treron No. 292; акценты эгейский синий S 3050-R80B, охра India Yellow No. 66, олива S 5020-G90Y. По брифу: дерево — дуб табак (мебель, лестница), фурнитура и светильники — латунь, рамы и металл — тёплый графит; свет тёплый 2700–3000 K, фасады матовые. Цветовая схема — комплементарная, пропорция 60/30/10: база на стенах и потолках, вторичный цвет — в текстиле и мягкой мебели, акцент — точечно.

Мудборд: материалы и фактуры

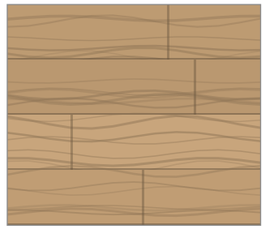

1167-4250
пол

A8UZ
пол, стены

Loft White · Little Greene No. 222
потолок, стены, плинтус

Calla · Tikkurila G503
стены, плинтус

NCS S 0502-Y
стены

NCS S 0300-N
потолок, плинтус

Lulworth Blue — светлая морская лазурь · Farrow & Ball No. 89
акцент (стена А)

India Yellow — охра / горчица итальянских фасадов · Farrow & Ball No. 66
акцент (стена А)

Tikkurila H440
акцент (стена А)

Палитра 60/30/10

60 % база — Tikkurila G503 Calla, LRV 89; Farrow & Ball No. 239 Wimborne White — белый с каплей тёплой охры, LRV 89; Little Greene No. 222 Loft White, LRV 92

30 % вторичный — NCS S 1010-Y20R Светлый песок / известняк, LRV 75; Farrow & Ball No. 89 Lulworth Blue — светлая морская лазурь, LRV 45; Farrow & Ball No. 292 Treron — серо-оливковая листва, LRV 15

10 % акцент — NCS S 3050-R80B Эгейский синий, LRV 13; Farrow & Ball No. 66 India Yellow — охра / горчица итальянских фасадов, LRV 36; NCS S 5020-G90Y Олива, LRV 20

Функциональное зонирование (М 1:200)

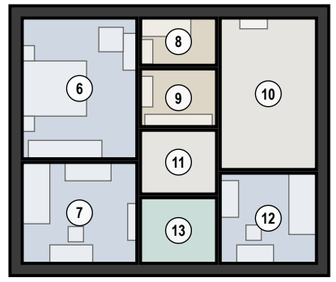

- ночная зона: спальни
- мокрая зона: санузлы
- хранение: гардеробная, кладовая
- вход и коммуникации
- (1) номер помещения (лист 22)

Образы помещений

6. Спальня родителей — 17,17 м²

стены Tikkurila G503; акцент No. 89 на стене А
пол — 1167-4250
текстиль: портьеры S 1010-Y20R, тюль No. 222, ковёр X395
декор: картина над кроватью, Аглаонема в кашпо
свет 2700 K, сценарии: вечер, уборка

7. Детская — 12,30 м²

стены Tikkurila G503; акцент No. 66 на стене А
пол — 1167-4250
текстиль: портьеры S 1010-Y20R, тюль No. 222, ковёр X463
декор: картина над кроватью, зеркало в рост
свет 2700 K, сценарии: вечер

12. Детская вторая — 9,23 м²

стены Tikkurila G503; акцент H440 на стене А
пол — 1167-4250
текстиль: портьеры S 1010-Y20R, тюль No. 222, ковёр X463
декор: картина над кроватью, зеркало в рост
свет 2700 K, сценарии: вечер

10. Холл второго этажа — 15,51 м²

стены Tikkurila G503
пол — 1167-4250
декор: Хлорофитум в кашпо
свет 3000 K

11. Коридор второго этажа — 5,16 м²

стены Tikkurila G503
пол — 1167-4250
декор: Сансевиерия в кашпо
свет 3000 K

8. Гардеробная — 3,82 м²

стены Little Greene No. 222
пол — 1167-4250
свет 3000 K

13. Санузел второго этажа — 5,31 м²

стены Atlas Concorde A8UZ
пол — A8UZ
декор: зеркало над умывальником
свет 3000 K

9. Кладовая — 4,66 м²

стены NCS S 0502-Y
пол — 1167-4250
свет 3000 K

Материалы и отделка

1167-4250
пол — пом. 6, 7, 8, 9, 10, 11, 12

A8UZ
пол, стены — пом. 13

Tikkurila G503 Calla, LRV 89
Farrow & Ball Modern Emulsion, матовая
стены, плинтус — пом. 6, 7, 10, 11, 12

Little Greene No. 222 Loft White, LRV 92
Tikkurila Anti-Reflex 2, глубокоматовая
потолок, стены, плинтус — пом. 6, 7, 8, 10, 11, 12, 13

NCS S 0502-Y, LRV 86
матовая
стены — пом. 9

NCS S 0300-N, LRV 92
глубокоматовая
потолок, плинтус — пом. 9

Farrow & Ball No. 89 Lulworth Blue — светлая морская лазурь, LRV 45
акцентная стена
акцент (стена А) — пом. 6

Farrow & Ball No. 66 India Yellow — охра / горчица итальянских фасадов, LRV 36
акцентная стена
акцент (стена А) — пом. 7

Tikkurila H440, LRV 51
акцентная стена
акцент (стена А) — пом. 12

Текстиль и металл

Лён, NCS S 1010-Y20R
портьеры-волна, подушки декоративные на кровать

Шерсть, Tikkurila X395
ковёр под кроватью

Шерсть, Farrow & Ball No. 89
плед на кровать

Букле, NCS S 1010-Y20R
подушки декоративные на кровать

Шерсть, Farrow & Ball No. 66
плед на кровать

Вуаль, Little Greene No. 222
тюль

Бархат, Farrow & Ball No. 89
подушки на кровать

Шерсть, Tikkurila X463
ковёр под кроватью

Бархат, Farrow & Ball No. 66
подушки на кровать

Чёрный матовый металл
зеркало в рост

Чего избегаем

1) Глянец и пластик под камень
2) Холодный белый 6500 K и LED-ленты холодного оттенка
3) Ракушки, якоря, штурвалы толпой — это морской китч, не средиземноморье
4) Ярко-синие стены в северной комнате без тёплой основы
5) Глянцевая кафельная плитка под котто
6) Тяжёлые портьеры и ламбрекены

Допущения и предложения на листе

Основа листа: взаимное расположение помещений, контур дома 9600 × 8000 и раскладка этажей подобраны проектировщиком под габариты помещений брифа; обмер и проект АР — задание (К-1); высота потолка 2900 мм — по брифу, не замерена; перекрытие 330 мм и отметка 2-го этажа +3,230 приняты; проект КР — задание (К-2); наружные стены 400 мм, перегородки 120 мм приняты (в брифе толщин нет) (К-1); разрешённая мощность 15 кВт принята по типовым ТУ для частного дома (К-4).

Примечания

См. лист открытых вопросов (лист 6, записи К-1, К-2, К-4).

1. Коды цвета — по веерам производителей (колерная карта, лист 62); перед закупкой краски — выкрас на стене объекта под дневным светом и лампами проекта.
2. Материалы — по ведомости отделки (лист 60); мебель, текстиль и декор — по спецификации (лист 24). Образцы доски, керамогранита и тканей утвердить до заказа.
3. Фактуры на листе условные, цвет передан по HEX-значениям производителей: при печати возможны отклонения, решение — только по физическому образцу.

Изм.	Кол.уч	Лист	№ док.	Подп.	Дата
Разраб.		Кырлан А.С.			19.10.26
Пров.					
ГИП					
Н. контр.					
Утв.					

ГД-2026-012-АИ

Дом 120 м²

Общая площадь 147,36* м² · * размеры приняты, не замерены (реестр — л. 6, К-1)

Дизайн-проект интерьера	Стадия	Лист	Листов
	РП	21	130

Концепция интерьера · 2-й этаж

М б/м

Кырлан Александр Сергеевич

выпуск 19.10.2026 № 53e4f7ddae · стр. 23 из 160

План расстановки мебели · 1-й этаж

Мебель и оборудование · размеры в мм от чистовых стен · марки — по ведомости

ПРЕДВАРИТЕЛЬНО · не для производства работ · открыто пунктов: 6 (реестр — л. 6)

Условные обозначения

- мебель и оборудование — габарит в масштабе
- навесные шкафы (низ выше 0,9 м) — невидимый контур
- ковёр
- зона открывания дверец шкафов и техники
- К1 — марка предмета по ведомости мебели
- привязка от чистовой стены, мм
- ширина прохода, зазор, мм
- сантехприборы — подложка (лист ВК)
- радиатор отопления (лист ОВ)
- существующие стены (сечение)
- стояк: К1 — канализация, В1 — ХВС, Т3 — ГВС
- 1 — номер помещения, площадь м²
- *зона* — функциональная зона помещения

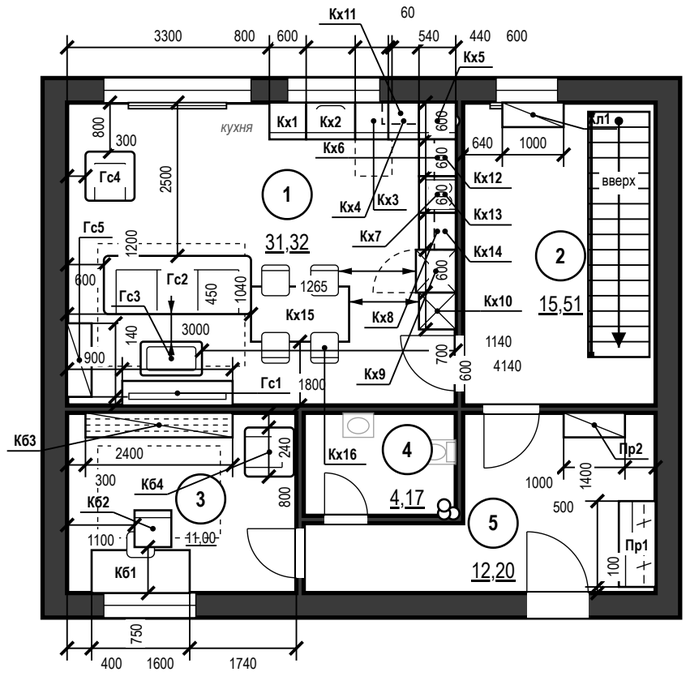

Примечания

1. Размеры даны в мм от чистовых поверхностей стен: слой штукатурки 20 мм по блоку и 5 мм шпаклёвки по ГКЛ учтён. Перед заказом встроенной мебели контрольный обмер после штукатурки.
2. Привязки мебели — от стен и углов помещения, а не от другой мебели; ширина проходов и зазоров показана стрелками.
3. Розетки, выводы и выключатели под мебель — см. лист 28 «План розеток и электровыводов · 1-й этаж»; сантехприборы и выводы воды — лист 46.
4. План расстановки не является документацией для изготовления мебели: изделия — по чертежам мебельщика; покупную мебель заменять только на изделия не больше габарита из спецификации (лист 24).
5. Встроенная мебель «стена в стену» — с зазором 10 мм с каждой стороны или с компенсаторами.
6. Отступ от стены, на плане не образмерен: Кб4 — 40 мм.
7. Стулья обеденной группы (Кх16 — 4 шт.) показаны в рабочем положении, задвинутыми под столешницу на 150 мм.

Экспликация помещений

лист 13 · на плане — номера в марках

Ведомость мебели и оборудования

Марка	Наименование	Ш×Г×В, мм	Пом.	Кол.
Кх1	Модуль с ящиками	600×600×900	1	1
Кх2	Модуль под мойку у окна	800×600×900	1	1
Кх3	Посудомоечная машина встроенная	600×600×900	1	1
Кх4	Модуль с ящиками	500×600×900	1	1
Кх5	Модуль угловой с каруселью	600×600×900	1	1
Кх6	Модуль с ящиками	600×600×900	1	1
Кх7	Модуль с варочной панелью	600×600×900	1	1
Кх8	Модуль с ящиками	600×600×900	1	1
Кх9	Колонна с холодильником	700×650×2200	1	1
Кх10	Пенал-кладовая с выдвижными корзинами	600×600×2200	1	1
Кх11	Навесной шкаф у окна	600×350×900	1	1
Кх12	Навесной шкаф	600×350×900	1	1
Кх13	Вытяжка встраиваемая в навесной	600×350×900	1	1
Кх14	Навесной шкаф с сушкой для посуды	600×350×900	1	1
Кх15	Стол обеденный 1600×900	1600×900×750	1	1
Гс1	ТВ-тумба подвесная с экраном	1800×400×600	1	1
Гс2	Диван трёхместный	2400×950×820	1	1
Гс3	Столик журнальный	1000×550×420	1	1
Гс4	Кресло у окна	800×800×850	1	1
Гс5	Буфет низкий	1200×400×800	1	1
Хл1	Банкетка под окном	1000×400×450	2	1
Кб1	Стол письменный у окна	1600×700×750	3	1
Кб2	Кресло рабочее	600×600×900	3	1
Кб3	Стеллаж для книг во всю стену	2400×400×2400	3	1
Кб4	Кресло для чтения	800×800×850	3	1
Пр1	Шкаф-купе до потолка	1400×600×2800	5	1
Пр2	Банкетка-обувница	1000×400×450	5	1
Кх16	Стул обеденный к столу Кх15	450×500×820	1	4

Ш — вдоль стены (изголовья), Г — от стены (длина кровати)

Материалы, модели, допуск замены — лист 24

Допущения и предложения на листе

Основа листа: взаимное расположение помещений, контур дома 9600 × 8000 и раскладка этажей подобраны проектировщиком под габариты помещений брифа; обмер и проект АР — задание (К-1); высота потолка 2900 мм — по брифу, не замерена; перекрытие 330 мм и отметка 2-го этажа +3,230 приняты; проект КР — задание (К-2); наружные стены 400 мм, перегородки 120 мм приняты (в брифе толщин нет) (К-1); разрешённая мощность 15 кВт принята по типовым ТУ для частного дома (К-4).

Открытые вопросы и конфликты по листу: К-1.

См. лист открытых вопросов (лист 6, записи К-1, К-2, К-4).

1000 мм · печать 1:1

Изм.	Кол.уч	Лист	№ док.	Подп.	Дата
Разраб.		Кырлан А.С.			19.10.26
Пров.					
ГИП					
Н. контр.					
Утв.					

ГД-2026-012-АИ

Дом 120 м²

Общая площадь 147,36* м² · * размеры приняты, не замерены (реестр — л. 6, К-1)

Дизайн-проект интерьера

Стадия	Лист	Листов
РП	22	130

План расстановки мебели · 1-й этаж

М 1:100

Кырлан Александр Сергеевич

выпуск 19.10.2026 № 53e4f7ddae · стр. 24 из 160

План расстановки мебели · 2-й этаж

Мебель и оборудование · размеры в мм от чистовых стен · марки — по ведомости

Условные обозначения

- мебель и оборудование — габарит в масштабе
- навесные шкафы (низ выше 0,9 м) — невидимый контур
- ковёр
- зона открывания дверец шкафов и техники
- К1 — марка предмета по ведомости мебели
- привязка от чистовой стены, мм
- ширина прохода, зазор, мм
- сантехприборы — подложка (лист ВК)
- радиатор отопления (лист ОВ)
- существующие стены (сечение)
- стояк: К1 — канализация, В1 — ХВС, Т3 — ГВС
- (1) — номер помещения, площадь м²

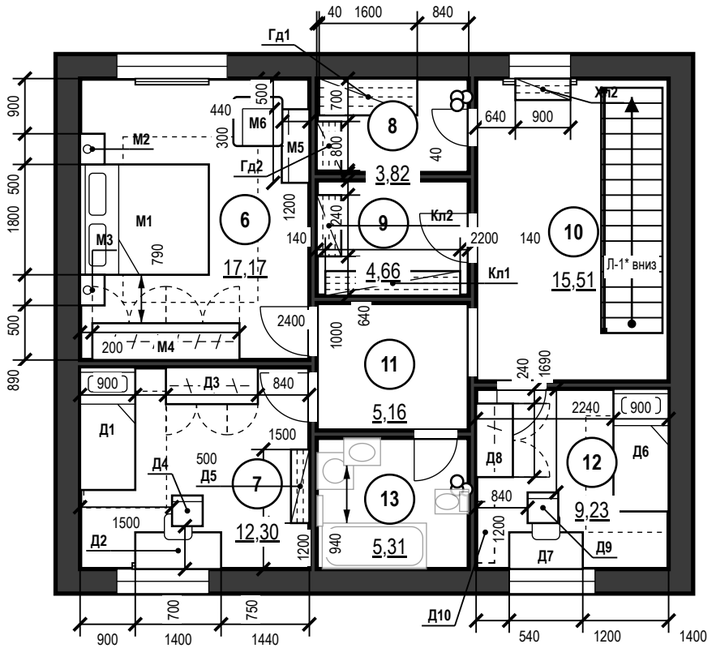

Примечания

1. Размеры даны в мм от чистовых поверхностей стен: слой штукатурки 20 мм по блоку и 5 мм шпаклёвки по ГКЛ учтён. Перед заказом встроенной мебели контрольный обмер после штукатурки.
2. Привязки мебели — от стен и углов помещения, а не от другой мебели; ширина проходов и зазоров показана стрелками.
3. Розетки, выводы и выключатели под мебель — см. лист 28 «План розеток и электровыводов · 1-й этаж»; сантехприборы и выводы воды — лист 46.
4. План расстановки не является документацией для изготовления мебели: изделия — по чертежам мебельщика; покупную мебель заменять только на изделия не больше габарита из спецификации (лист 24).
5. Встроенная мебель «стена в стену» — с зазором 10 мм с каждой стороны или с компенсаторами.

Экспликация помещений

лист 13 · на плане — номера в марках

Ведомость мебели и оборудования

Марка	Наименование	Ш×Г×В, мм	Пом.	Кол.
М1	Кровать 1800×2000 с мягким	1800×2100×1100	6	1
М2	Тумба прикроватная	500×400×550	6	1
М3	Тумба прикроватная	500×400×550	6	1
М4	Шкаф распашной до потолка	2400×600×2600	6	1
М5	Комод	1200×450×800	6	1
М6	Кресло у окна	800×800×850	6	1
Д1	Кровать 900×2000 с бортиком	900×2000×450	7	1
Д2	Стол письменный у окна	1400×600×750	7	1
Д3	Шкаф распашной	1500×600×2200	7	1
Д4	Стул растущий	500×500×800	7	1
Д5	Стеллаж для книг и игрушек	1200×300×1600	7	1
Гд1	Система хранения	1600×600×2600	8	1
Гд2	Полки для обуви и сумок	800×400×2000	8	1
Кл1	Стеллаж для хранения	2200×400×2200	9	1
Кл2	Стеллаж узкий для бытовой техники	1000×400×2200	9	1
Хл2	Стеллаж-библиотека низкий под окном	900×350×850	10	1
Д6	Кровать 900×2000 с бортиком	900×2000×450	12	1
Д7	Стол письменный у окна	1200×600×750	12	1
Д8	Шкаф распашной	1200×600×2200	12	1
Д9	Стул растущий	500×500×800	12	1
Д10	Полки открытые над столом	1000×300×1200	12	1

Ш — вдоль стены (изголовья), Г — от стены (длина кровати)

Материалы, модели, допуск замены — лист 24

Допущения и предложения на листе

Основа листа: взаимное расположение помещений, контур дома 9600 × 8000 и раскладка этажей подобраны проектировщиком под габариты помещений брифа; обмер и проект АР — задание (К-1); высота потолка 2900 мм — по брифу, не замерена; перекрытие 330 мм и отметка 2-го этажа +3,230 приняты; проект КР — задание (К-2); наружные стены 400 мм, перегородки 120 мм приняты (в брифе толщин нет) (К-1); разрешённая мощность 15 кВт принята по типовым ТУ для частного дома (К-4).

Знак «*» — принято, не замерено и не подтверждено (замерить на объекте): К-3: Л-1 — место, тип и размеры лестницы брифом не заданы (только «лестница из холла 1-го этажа»): одномаршевая 17 × 190 × 250 вдоль стены Б холла — предложение проектировщика; конструкция и расчёт — проект КР.

Открытые вопросы и конфликты по листу: К-1.

См. лист открытых вопросов (лист 6, записи К-1–К-4).

1000 мм · печать 1:1

Изм.	Кол.уч	Лист	№ док.	Подп.	Дата
Разраб.		Кырлан А.С.			19.10.26
Пров.					
ГИП					
Н. контр.					
Утв.					

ГД-2026-012-АИ

Дом 120 м²

Общая площадь 147,36* м² · * размеры приняты, не замерены (реестр — л. 6, К-1)

Дизайн-проект интерьера

Стадия	Лист	Листов
РП	23	130

План расстановки мебели · 2-й этаж

М 1:100

Кырлан Александр Сергеевич

01

Планировочное решение

Кырлан Александр Сергеевич

выпуск 19.10.2026 № 53e4f7ddae · стр. 26 из 160

Спецификация мебели и оборудования

ПРЕДВАРИТЕЛЬНО · не для производства работ · открыто пунктов: 6 (реестр — л. 6)

Форма 1 ГОСТ 21.110-2013 · позиции мебели — по плану расстановки

Поз.	Наименование и техническая характеристика	Тип, марка, обозначение документа, опросного листа	Код продукции	Поставщик	Ед. измерения	Кол.	Масса 1 ед., кг	Примечание
	Мебель встроенная и корпусная (изготовление по чертежам мебельщика)							
Кх1	Модуль с ящиками; корпус ЛДСП, фасады — матовая эмаль в тон стен; Ш×Г×В 600×600×900 мм			изготовление на заказ	шт.	1		пом. 1
Кх2	Модуль под мойку у окна; корпус ЛДСП, фасады — матовая эмаль в тон стен; Ш×Г×В 800×600×900 мм			изготовление на заказ	шт.	1		пом. 1
Кх3	Посудомоечная машина встроенная; корпус ЛДСП, фасады — матовая эмаль в тон стен; Ш×Г×В 600×600×900 мм			изготовление на заказ	шт.	1		пом. 1
Кх4	Модуль с ящиками; корпус ЛДСП, фасады — матовая эмаль в тон стен; Ш×Г×В 500×600×900 мм			изготовление на заказ	шт.	1		пом. 1
Кх5	Модуль угловой с каруселью; корпус ЛДСП, фасады — матовая эмаль в тон стен; Ш×Г×В 600×600×900 мм			изготовление на заказ	шт.	1		пом. 1
Кх6	Модуль с ящиками; корпус ЛДСП, фасады — матовая эмаль в тон стен; Ш×Г×В 600×600×900 мм			изготовление на заказ	шт.	1		пом. 1
Кх7	Модуль с варочной панелью и духовым шкафом; корпус ЛДСП, фасады — матовая эмаль в тон стен; Ш×Г×В 600×600×900 мм			изготовление на заказ	шт.	1		пом. 1
Кх8	Модуль с ящиками; корпус ЛДСП, фасады — матовая эмаль в тон стен; Ш×Г×В 600×600×900 мм			изготовление на заказ	шт.	1		пом. 1
Кх9	Колонна с холодильником; корпус ЛДСП, фасады — матовая эмаль в тон стен; Ш×Г×В 700×650×2200 мм			изготовление на заказ	шт.	1		пом. 1
Кх10	Пенал-кладовая с выдвижными корзинами; корпус ЛДСП, фасады — матовая эмаль в тон стен; Ш×Г×В 600×600×2200 мм			изготовление на заказ	шт.	1		пом. 1
Кх11	Навесной шкаф у окна, витрина со стеклом; корпус ЛДСП, фасады — матовая эмаль в тон стен; Ш×Г×В 600×350×900 мм			изготовление на заказ	шт.	1		пом. 1
Кх12	Навесной шкаф, фасад в тон цоколя; корпус ЛДСП, фасады — матовая эмаль в тон стен; Ш×Г×В 600×350×900 мм			изготовление на заказ	шт.	1		пом. 1
Кх13	Вытяжка встраиваемая в навесной шкаф; корпус ЛДСП, фасады — матовая эмаль в тон стен; Ш×Г×В 600×350×900 мм			изготовление на заказ	шт.	1		пом. 1
Кх14	Навесной шкаф с сушкой для посуды; корпус ЛДСП, фасады — матовая эмаль в тон стен; Ш×Г×В 600×350×900 мм			изготовление на заказ	шт.	1		пом. 1
Пр1	Шкаф-купе до потолка, дуб табак; корпус ЛДСП, фасады — матовая эмаль в цвет стен (Tikkurila G503); Ш×Г×В 1400×600×2800 мм			изготовление на заказ	шт.	1		пом. 5
М4	Шкаф распашной до потолка, фасады матовые; корпус ЛДСП, фасады — матовая эмаль в цвет стен (Tikkurila G503); Ш×Г×В 2400×600×2600 мм			изготовление на заказ	шт.	1		пом. 6
Д3	Шкаф распашной; корпус ЛДСП, фасады — матовая эмаль в цвет стен (Tikkurila G503); Ш×Г×В 1500×600×2200 мм			изготовление на заказ	шт.	1		пом. 7
Гд1	Система хранения: штанги, полки, ящики; каркас и полки — ЛДСП, декор «дуб натуральный»; Ш×Г×В 1600×600×2600 мм			изготовление на заказ	шт.	1		пом. 8; крепление к стене
Гд2	Полки для обуви и сумок; каркас и полки — ЛДСП, декор «дуб натуральный»; Ш×Г×В 800×400×2000 мм			изготовление на заказ	шт.	1		пом. 8; крепление к стене
Д8	Шкаф распашной; корпус ЛДСП, фасады — матовая эмаль в цвет стен (Tikkurila G503); Ш×Г×В 1200×600×2200 мм			изготовление на заказ	шт.	1		пом. 12
	Мебель покупная							
Гс1	ТВ-тумба подвесная с экраном, дуб табак; шпон, дуб натуральный, матовое масло; Ш×Г×В 1800×400×600 мм			аналог по характеристикам	шт.	1		пом. 1; замена ≤ габарита
Гс2	Диван трёхместный, лён; обивка — ткань, цвет NCS S 1010-Y20R; Ш×Г×В 2400×950×820 мм			аналог по характеристикам	шт.	1		пом. 1; замена ≤ габарита
Гс3	Столик журнальный, дуб и латунь; шпон, дуб натуральный, матовое масло; Ш×Г×В 1000×550×420 мм			аналог по характеристикам	шт.	1		пом. 1; замена ≤ габарита
Гс4	Кресло у окна, букле; обивка — ткань, цвет NCS S 1010-Y20R; Ш×Г×В 800×800×850 мм			аналог по характеристикам	шт.	1		пом. 1; замена ≤ габарита
Гс5	Буфет низкий, дуб табак; шпон, дуб натуральный, матовое масло; Ш×Г×В 1200×400×800 мм			аналог по характеристикам	шт.	1		пом. 1; крепление к стене; замена ≤ габарита
Кх15	Стол обеденный 1600×900, дуб табак; шпон, дуб натуральный, матовое масло; Ш×Г×В 1600×900×750 мм			аналог по характеристикам	шт.	1		пом. 1; замена ≤ габарита
Кх16	Стул обеденный к столу Кх15; обивка — ткань, цвет NCS S 1010-Y20R; каркас — дуб натуральный; Ш×Г×В 450×500×820 мм			аналог по характеристикам	шт.	4		пом. 1; замена ≤ габарита

Примечания

1. Позиции мебели совпадают с марками на плане расстановки (лист 22); размеры Ш×Г×В — Ш вдоль стены, Г от стены.
2. Встроенная и корпусная мебель изготавливается по чертежам мебельщика после контрольного обмера; графы «Тип, марка» и «Код продукции» для неё не заполняются (ГОСТ 21.110-2013).
3. Покупные изделия — аналог по характеристикам: заменять только на изделия не больше указанного габарита и того же материала и цвета.
4. Материал и цвет, не указанные в данных изделия, приняты по концепции (лист 20): тон дерева — по полу, обивка — по вторичному цвету палитры; образцы согласовать до заказа.
5. Масса 1 ед. для изделий до 25 кг не указывается. Техника — по монтажным схемам изготовителя; выводы — по листам ЭОМ и ВК.

Допущения и предложения на листе

Основа листа: взаимное расположение помещений, контур дома 9600 × 8000 и раскладка этажей подобраны проектировщиком под габариты помещений брифа; обмер и проект АР — задание (К-1); высота потолка 2900 мм — по брифу, не замерена; перекрытие 330 мм и отметка 2-го этажа +3,230 приняты; проект КР — задание (К-2); наружные стены 400 мм, перегородки 120 мм приняты (в брифе толщин нет) (К-1); разрешённая мощность 15 кВт принята по типовым ТУ для частного дома (К-4).
См. лист открытых вопросов (лист 6, записи К-1, К-2, К-4).

Изм.	Кол.уч	Лист	№ док.	Подп.	Дата
Разраб.		Кырлан А.С.			19.10.26
Пров.					
ГИП					
Н. контр.					
Утв.					

ГД-2026-012-АИ

Дом 120 м²

Общая площадь 147,36* м² · * размеры приняты, не замерены (реестр — л. 6, К-1)

Дизайн-проект интерьера

Стадия	Лист	Листов
РП	24	130

Спецификация мебели и оборудования

М б/м

Кырлан Александр Сергеевич

выпуск 19.10.2026 № 53e4f7ddae · стр. 27 из 160

Спецификация мебели и оборудования (продолжение)

Форма 1 ГОСТ 21.110-2013 · позиции мебели — по плану расстановки

ПРЕДВАРИТЕЛЬНО · не для производства работ · открыто пунктов: 6 (реестр — л. 6)

Поз.	Наименование и техническая характеристика	Тип, марка, обозначение документа, опросного листа	Код продукции	Поставщик	Ед. измерения	Кол.	Масса 1 ед., кг	Примечание
Хл1	Банкетка под окном, дуб табак; Ш×Г×В 1000×400×450 мм			аналог по характеристикам	шт.	1		пом. 2; замена ≤ габарита
Кб1	Стол письменный у окна, дуб табак; шпон, дуб натуральный, матовое масло; Ш×Г×В 1600×700×750 мм			аналог по характеристикам	шт.	1		пом. 3; замена ≤ габарита
Кб2	Кресло рабочее; обивка — ткань, цвет NCS S 1010-Y20R; каркас — дуб натуральный; Ш×Г×В 600×600×900 мм			аналог по характеристикам	шт.	1		пом. 3; замена ≤ габарита
Кб3	Стеллаж для книг во всю стену; шпон, дуб натуральный, матовое масло; Ш×Г×В 2400×400×2400 мм			аналог по характеристикам	шт.	1		пом. 3; крепление к стене; замена ≤ габарита
Кб4	Кресло для чтения; обивка — ткань, цвет NCS S 1010-Y20R; Ш×Г×В 800×800×850 мм			аналог по характеристикам	шт.	1		пом. 3; замена ≤ габарита
Пр2	Банкетка-обувница; Ш×Г×В 1000×400×450 мм			аналог по характеристикам	шт.	1		пом. 5; замена ≤ габарита
М1	Кровать 1800×2000 с мягким изголовьем 1100, лён; мягкое изголовье, обивка — ткань, цвет NCS S 1010-Y20R; Ш×Г×В 1800×2100×1100 мм			аналог по характеристикам	шт.	1		пом. 6; замена ≤ габарита
М2, М3	Тумба прикроватная, дуб табак; шпон, дуб натуральный, матовое масло; Ш×Г×В 500×400×550 мм			аналог по характеристикам	шт.	2		пом. 6; замена ≤ габарита
М5	Комод, дуб табак; шпон, дуб натуральный, матовое масло; Ш×Г×В 1200×450×800 мм			аналог по характеристикам	шт.	1		пом. 6; крепление к стене; замена ≤ габарита
М6	Кресло у окна; обивка — ткань, цвет NCS S 1010-Y20R; Ш×Г×В 800×800×850 мм			аналог по характеристикам	шт.	1		пом. 6; замена ≤ габарита
Д1, Д6	Кровать 900×2000 с бортиком; мягкое изголовье, обивка — ткань, цвет NCS S 1010-Y20R; Ш×Г×В 900×2000×450 мм			аналог по характеристикам	шт.	2		пом. 7, 12; замена ≤ габарита
Д2	Стол письменный у окна; шпон, дуб натуральный, матовое масло; Ш×Г×В 1400×600×750 мм			аналог по характеристикам	шт.	1		пом. 7; замена ≤ габарита
Д4, Д9	Стул растущий; обивка — ткань, цвет NCS S 1010-Y20R; каркас — дуб натуральный; Ш×Г×В 500×500×800 мм			аналог по характеристикам	шт.	2		пом. 7, 12; замена ≤ габарита
Д5	Стеллаж для книг и игрушек; шпон, дуб натуральный, матовое масло; Ш×Г×В 1200×300×1600 мм			аналог по характеристикам	шт.	1		пом. 7; крепление к стене; замена ≤ габарита
Кл1	Стеллаж для хранения; каркас и полки — ЛДСП, декор «дуб натуральный»; Ш×Г×В 2200×400×2200 мм			аналог по характеристикам	шт.	1		пом. 9; крепление к стене; замена ≤ габарита
Кл2	Стеллаж узкий для бытовой техники; каркас и полки — ЛДСП, декор «дуб натуральный»; Ш×Г×В 1000×400×2200 мм			аналог по характеристикам	шт.	1		пом. 9; крепление к стене; замена ≤ габарита
Хл2	Стеллаж-библиотека низкий под окном; шпон, дуб натуральный, матовое масло; Ш×Г×В 900×350×850 мм			аналог по характеристикам	шт.	1		пом. 10; крепление к стене; замена ≤ габарита
Д7	Стол письменный у окна; шпон, дуб натуральный, матовое масло; Ш×Г×В 1200×600×750 мм			аналог по характеристикам	шт.	1		пом. 12; замена ≤ габарита
Д10	Полки открытые над столом; каркас и полки — ЛДСП, декор «дуб натуральный»; Ш×Г×В 1000×300×1200 мм			аналог по характеристикам	шт.	1		пом. 12; крепление к стене; замена ≤ габарита
	Техника встраиваемая и бытовая, светильники под розетки							
	Посудомоечная машина встраиваемая, в модуле Кх3; ниша 600 мм			аналог по характеристикам	шт.	1		пом. 1; по схеме изготовителя
	Варочная панель встраиваемая, электрическая, в модуле Кх7			аналог по характеристикам	шт.	1		пом. 1; по схеме изготовителя
	Духовой шкаф встраиваемый, в модуле Кх7			аналог по характеристикам	шт.	1		пом. 1; по схеме изготовителя
	Холодильник встраиваемый, в модуле Кх9			аналог по характеристикам	шт.	1		пом. 1; по схеме изготовителя
	Вытяжка встраиваемая, в модуле Кх13			аналог по характеристикам	шт.	1		пом. 1; по схеме изготовителя

Допущения и предложения на листе

Основа листа: взаимное расположение помещений, контур дома 9600 × 8000 и раскладка этажей подобраны проектировщиком под габариты помещений брифа; обмер и проект АР — задание (К-1); высота потолка 2900 мм — по брифу, не замерена; перекрытие 330 мм и отметка 2-го этажа +3,230 приняты; проект КР — задание (К-2); наружные стены 400 мм, перегородки 120 мм приняты (в брифе толщин нет) (К-1); разрешённая мощность 15 кВт принята по типовым ТУ для частного дома (К-4).

См. лист открытых вопросов (лист 6, записи К-1, К-2, К-4).

Изм.	Кол.уч	Лист	№ док.	Подп.	Дата
Разраб.		Кырлан А.С.			19.10.26
Пров.					
ГИП					
Н. контр.					
Утв.					

ГД-2026-012-АИ

Дом 120 м²

Общая площадь 147,36* м² · * размеры приняты, не замерены (реестр — л. 6, К-1)

Дизайн-проект интерьера

Стадия	Лист	Листов
РП	25	130

Спецификация мебели и оборудования (продолжение)

М б/м

Кырлан Александр Сергеевич

Спецификация мебели и оборудования (продолжение)

Форма 1 ГОСТ 21.110-2013 · позиции мебели — по плану расстановки

ПРЕДВАРИТЕЛЬНО · не для производства работ · открыто пунктов: 6 (реестр — л. 6)

Поз.	Наименование и техническая характеристика	Тип, марка, обозначение документа, опросного листа	Код продукции	Поставщик	Ед. измерения	Кол.	Масса 1 ед., кг	Примечание
	Стиральная машина, место по листу ВК (См3); Ш×Г 600×600 мм			аналог по характеристикам	шт.	1		пом. 13; по схеме изготовителя
	Торшер, у поз. Гс4; абажур — ткань или опаловое стекло; лампа 2700 K			аналог по характеристикам	шт.	1		пом. 1; розетка Р21 (ЭОМ)
	Торшер, у поз. М6; абажур — ткань или опаловое стекло; лампа 2700 K			аналог по характеристикам	шт.	1		пом. 6; розетка Р5 (ЭОМ)
	Текстиль							
Т13	Портьеры-волна (гостиная); лён 70 %, вискоза 30 %; цвет NCS S 1010-Y20R; карниз 3000 мм, высота 2870 мм, сборка 2			аналог по характеристикам	шт.	2		пом. 1
Т14	Тюль (гостиная); полиэстер 100 %; цвет Little Greene No. 222; карниз 3000 мм, высота 2870 мм, сборка 2,5			аналог по характеристикам	шт.	1		пом. 1
Т15	Римская штора (кухня); лён 100 %; цвет Tikkurila X463; карниз 1500 мм, высота 1600 мм			аналог по характеристикам	шт.	1		пом. 1
Т16	Ковёр в зоне отдыха; шерсть 100 %; цвет Tikkurila X463; 2400×2000 мм			аналог по характеристикам	шт.	1		пом. 1; с подложкой
Т17	Подушки на диван; букле (шерсть 60 %, полиэстер 40 %); цвет NCS S 1010-Y20R			аналог по характеристикам	шт.	3		пом. 1
Т18	Подушки на диван, акцент; хлопковый бархат 100 %; цвет NCS S 3050-R80B			аналог по характеристикам	шт.	2		пом. 1
Т19	Плед на диван; альпака 50 %, шерсть 50 %; цвет Tikkurila X463			аналог по характеристикам	шт.	1		пом. 1
Т7	Портьеры-волна; лён 100 %; цвет NCS S 1010-Y20R; карниз 2100 мм, высота 2870 мм, сборка 2			аналог по характеристикам	шт.	2		пом. 3
Т8	Тюль; полиэстер 100 %; цвет Little Greene No. 222; карниз 2100 мм, высота 2870 мм, сборка 2,5			аналог по характеристикам	шт.	1		пом. 3
Т9	Ковёр под кроватью; шерсть 100 %; цвет Tikkurila X463; 2000×1500 мм			аналог по характеристикам	шт.	1		пом. 3; с подложкой
Т10	Подушки декоративные на кровать; букле (шерсть 60 %, полиэстер 40 %); цвет NCS S 1010-Y20R			аналог по характеристикам	шт.	3		пом. 3
Т11	Подушки на кровать, акцент; хлопковый бархат 100 %; цвет NCS S 5020-G90Y			аналог по характеристикам	шт.	2		пом. 3
Т12	Плед на кровать; шерсть мериноса 100 %; цвет NCS S 5020-G90Y			аналог по характеристикам	шт.	1		пом. 3
Т1	Портьеры-волна; лён 100 %; цвет NCS S 1010-Y20R; карниз 2400 мм, высота 2870 мм, сборка 2			аналог по характеристикам	шт.	2		пом. 6
Т2	Тюль; полиэстер 100 %; цвет Little Greene No. 222; карниз 2400 мм, высота 2870 мм, сборка 2,5			аналог по характеристикам	шт.	1		пом. 6
Т3	Ковёр под кроватью; шерсть 80 %, хлопок 20 %; цвет Tikkurila X395; 2200×2700 мм			аналог по характеристикам	шт.	1		пом. 6; с подложкой
Т4	Подушки декоративные на кровать; лён 100 %; цвет NCS S 1010-Y20R			аналог по характеристикам	шт.	3		пом. 6
Т5	Подушки на кровать, акцент; хлопковый бархат 100 %; цвет Farrow & Ball No. 89			аналог по характеристикам	шт.	2		пом. 6
Т6	Плед на кровать; шерсть мериноса 100 %; цвет Farrow & Ball No. 89			аналог по характеристикам	шт.	1		пом. 6
Т20	Портьеры-волна; лён 100 %; цвет NCS S 1010-Y20R; карниз 2100 мм, высота 2870 мм, сборка 2			аналог по характеристикам	шт.	2		пом. 7
Т21	Тюль; полиэстер 100 %; цвет Little Greene No. 222; карниз 2100 мм, высота 2870 мм, сборка 2,5			аналог по характеристикам	шт.	1		пом. 7
Т22	Ковёр под кроватью; шерсть 100 %; цвет Tikkurila X463; 1350×1900 мм			аналог по характеристикам	шт.	1		пом. 7; с подложкой
Т23	Подушки декоративные на кровать; букле (шерсть 60 %, полиэстер 40 %); цвет NCS S 1010-Y20R			аналог по характеристикам	шт.	3		пом. 7
Т24	Подушки на кровать, акцент; хлопковый бархат 100 %; цвет Farrow & Ball No. 66			аналог по характеристикам	шт.	2		пом. 7
Т25	Плед на кровать; шерсть мериноса 100 %; цвет Farrow & Ball No. 66			аналог по характеристикам	шт.	1		пом. 7
Т26	Портьеры-волна; лён 100 %; цвет NCS S 1010-Y20R; карниз 2000 мм, высота 2870 мм, сборка 2			аналог по характеристикам	шт.	2		пом. 12

Допущения и предложения на листе

Основа листа: взаимное расположение помещений, контур дома 9600 × 8000 и раскладка этажей подобраны проектировщиком под габариты помещений брифа; обмер и проект АР — задание (К-1); высота потолка 2900 мм — по брифу, не замерена; перекрытие 330 мм и отметка 2-го этажа +3,230 приняты; проект КР — задание (К-2); наружные стены 400 мм, перегородки 120 мм приняты (в брифе толщин нет) (К-1); разрешённая мощность 15 кВт принята по типовым ТУ для частного дома (К-4).

См. лист открытых вопросов (лист 6, записи К-1, К-2, К-4).

Изм.	Кол.уч	Лист	№ док.	Подп.	Дата
Разраб.		Кырлан А.С.			19.10.26
Пров.					
ГИП					
Н. контр.					
Утв.					

ГД-2026-012-АИ

Дом 120 м²

Общая площадь 147,36* м² · * размеры приняты, не замерены (реестр — л. 6, К-1)

Дизайн-проект интерьера

Стадия	Лист	Листов
РП	26	130

Спецификация мебели и оборудования (продолжение)

М б/м

Кырлан Александр Сергеевич

Спецификация мебели и оборудования (продолжение)

Форма 1 ГОСТ 21.110-2013 · позиции мебели — по плану расстановки

ПРЕДВАРИТЕЛЬНО · не для производства работ · открыто пунктов: 6 (реестр — л. 6)

Поз.	Наименование и техническая характеристика	Тип, марка, обозначение документа, опросного листа	Код продукции	Поставщик	Ед. измерения	Кол.	Масса 1 ед., кг	Примечание
Т27	Тюль; полиэстер 100 %; цвет Little Greene No. 222; карниз 2000 мм, высота 2870 мм, сборка 2,5			аналог по характеристикам	шт.	1		пом. 12
Т28	Ковёр под кроватью; шерсть 100 %; цвет Tikkurila X463; 1350×1900 мм			аналог по характеристикам	шт.	1		пом. 12; с подложкой
Т29	Подушки декоративные на кровать; букле (шерсть 60 %, полиэстер 40 %); цвет NCS S 1010-Y20R			аналог по характеристикам	шт.	3		пом. 12
Т30	Подушки на кровать, акцент; хлопковый бархат 100 %; цвет Tikkurila H440			аналог по характеристикам	шт.	2		пом. 12
Т31	Плед на кровать; шерсть мериноса 100 %; цвет Tikkurila H440			аналог по характеристикам	шт.	1		пом. 12
	Декор							
ДК6	Картина над креслом: пейзаж, масло, рама — дуб табак; 1000×800 мм; центр на 1550 мм от пола			аналог по характеристикам	шт.	1	6	пом. 1; крепление: анкер, 2 шт.
ДК7	Растение в кашпо; 450×450 мм			аналог по характеристикам	шт.	1		пом. 1
ДК8	Ваза керамическая с ветками на обеденном столе; 200×350 мм; на Кх15			аналог по характеристикам	шт.	1		пом. 1
ДК40	Олива в кадке Ø450 у окна; 450×450 мм			аналог по характеристикам	шт.	1		пом. 1
ДК41	Сансевиерия в кашпо Ø400 под лестницей; 400×400 мм			аналог по характеристикам	шт.	1		пом. 2
ДК3	Картина над креслом: гравюра в паспарту, рама — графит; 550×450 мм; низ на 1050 мм от пола			аналог по характеристикам	шт.	1	4	пом. 3; крепление к стене
ДК9	Зеркало над умывальником, влагостойкое; 500×700 мм; низ на 1100 мм от пола			аналог по характеристикам	шт.	1	4	пом. 4; крепление к стене
ДК5	Зеркало; рама — чёрный матовый; 600×1800 мм; низ на 550 мм от пола			аналог по характеристикам	шт.	1	18	пом. 5; крепление: анкер, 4 шт.
ДК43	Замиокулькас в кашпо Ø350; 350×350 мм			аналог по характеристикам	шт.	1		пом. 5
ДК1	Картина над кроватью: акварель, рама — светлый дуб; 1000×700 мм; низ на 1300 мм от пола			аналог по характеристикам	шт.	1	4	пом. 6; крепление к стене
ДК44	Аглаонема в кашпо Ø400; 400×400 мм			аналог по характеристикам	шт.	1		пом. 6
ДК2	Картина над кроватью: детская иллюстрация, рама — белёный дуб; 600×450 мм; низ на 650 мм от пола			аналог по характеристикам	шт.	1	4	пом. 7; крепление к стене
ДК4	Зеркало в рост в тонкой чёрной раме; рама — чёрный матовый; 500×1600 мм; низ на 300 мм от пола			аналог по характеристикам	шт.	1	12	пом. 7; крепление: анкер для пустотелых оснований, 4 шт.
ДК45	Хлорофитум в кашпо Ø350 у окна; 350×350 мм			аналог по характеристикам	шт.	1		пом. 10
ДК46	Сансевиерия в кашпо Ø400; 400×400 мм			аналог по характеристикам	шт.	1		пом. 11
ДК10	Картина над кроватью: детский принт, рама — светлый ясень; 600×450 мм; низ на 650 мм от пола			аналог по характеристикам	шт.	1	4	пом. 12; крепление к стене
ДК11	Зеркало в рост в тонкой чёрной раме; рама — чёрный матовый; 500×1600 мм; низ на 300 мм от пола			аналог по характеристикам	шт.	1	12	пом. 12; крепление: анкер для пустотелых оснований, 4 шт.
ДК12	Зеркало над умывальником, влагостойкое; 600×750 мм; низ на 1100 мм от пола			аналог по характеристикам	шт.	1	4	пом. 13; крепление к стене

Допущения и предложения на листе

Основа листа: взаимное расположение помещений, контур дома 9600 × 8000 и раскладка этажей подобраны проектировщиком под габариты помещений брифа; обмер и проект АР — задание (К-1); высота потолка 2900 мм — по брифу, не замерена; перекрытие 330 мм и отметка 2-го этажа +3,230 приняты; проект КР — задание (К-2); наружные стены 400 мм, перегородки 120 мм приняты (в брифе толщин нет) (К-1); разрешённая мощность 15 кВт принята по типовым ТУ для частного дома (К-4).

См. лист открытых вопросов (лист 6, записи К-1, К-2, К-4).

Изм.	Кол.уч	Лист	№ док.	Подп.	Дата
Разраб.		Кырлан А.С.			19.10.26
Пров.					
ГИП					
Н. контр.					
Утв.					

ГД-2026-012-АИ

Дом 120 м²

Общая площадь 147,36* м² · * размеры приняты, не замерены (реестр — л. 6, К-1)

Дизайн-проект интерьера	Стадия	Лист	Листов
	РП	27	130
Спецификация мебели и оборудования (продолжение) М б/м	**Кырлан Александр Сергеевич**		

План розеток и электровыводов · 1-й этаж

Розетки, выводы кабеля, щит · размеры в мм · высоты от чистого пола

ПРЕДВАРИТЕЛЬНО · не для производства работ · открыто пунктов: 6 (реестр — л. 6)

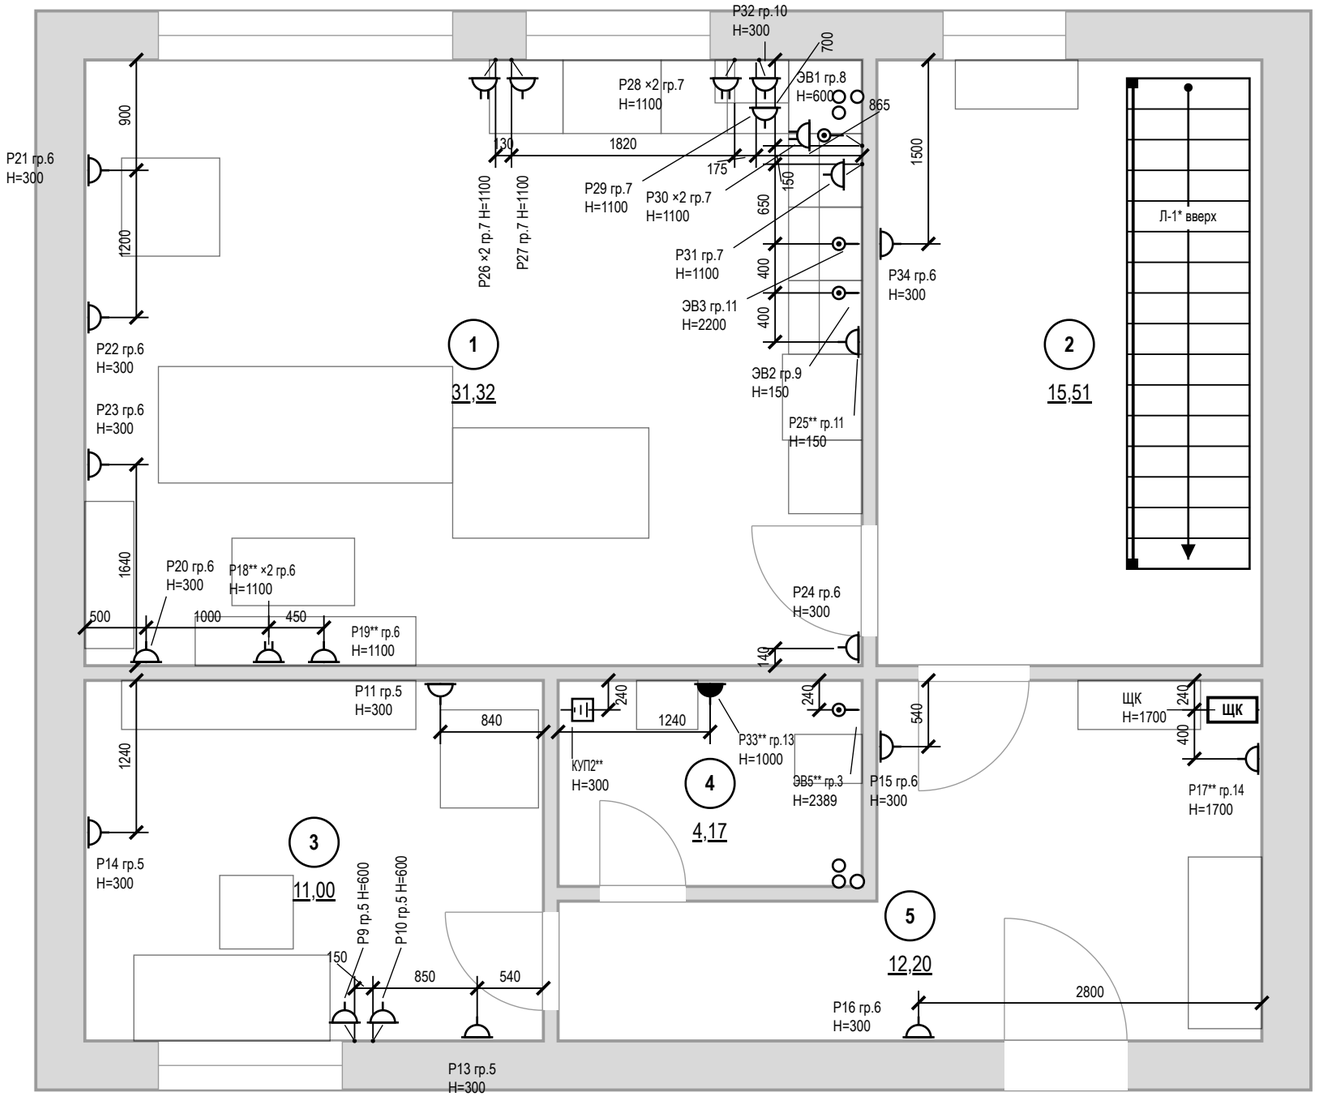

Условные обозначения

- розетка с заземляющим контактом; у знака — марка, ×N постов в рамке, гр. — группа щита, Н — высота оси, мм
- то же, рамка на 2 поста (число черточек — число постов)
- розетка влагозащищённая IP44
- вывод кабеля для подключения прибора (без розетки), марка ЭВ
- КУП — коробка уравнивания потенциалов (ДСУП), проводник к шине РЕ щита
- ЩК — щит квартирный
- знак разведён для читаемости: точка на стене — у выноски, привязка — до неё
- мебель и сантехприборы — подложка
- стояк: К1 — канализация, В1 — ХВС, Т3 — ГВС
- 1 — номер помещения, площадь м²

Допущения и предложения на листе

Основа листа: взаимное расположение помещений, контур дома 9600 × 8000 и раскладка этажей подобраны проектировщиком под габариты помещений брифа; обмер и проект АР — задание (К-1); высота потолка 2900 мм — по брифу, не замерена; перекрытие 330 мм и отметка 2-го этажа +3,230 приняты; проект КР — задание (К-2); наружные стены 400 мм, перегородки 120 мм приняты (в брифе толщин нет) (К-1); разрешённая мощность 15 кВт принята по типовым ТУ для частного дома (К-4).

Знак «*» — принято, не замерено и не подтверждено (замерить на объекте): К-3: Л-1 — место, тип и размеры лестницы брифом не заданы (только «лестница из холла 1-го этажа»): одномаршевая 17 × 190 × 250 вдоль стены Б холла — предложение проектировщика; конструкция и расчёт — проект КР.

Знак «**» — предложение проектировщика, заказчиком не утверждено (согласовать с заказчиком): записи в реестре нет: Р18 — высота 1100 мм выше нормы 1 м (ПУЭ 6.6.30) по назначению: питание ТВ, в одной зоне с выводами ТВ1 и LAN3; Р19 — высота 1100 мм выше нормы 1 м (ПУЭ 6.6.30) по назначению: питание приставки ТВ, в одной зоне с выводами ТВ1 и LAN3; Р25 — высота 2000 мм выше нормы 1 м (ПУЭ 6.6.30) по назначению: питание встроенного холодильника М6, розетка над нишей за съёмной панелью; Р33 — по образцу: Розетка Р33 на высоте 1100 мм, вне шва плитки; ЭВ5, КУП2 — по образцу: Добавлены выводы к вентиляторам: ЭВ4 (ВР1, ванная) и ЭВ5 (ВР3, санузел 2) — группа 3, высота 2389 мм, включение с основным светом, таймер выбега в вентиляторе; и коробки уравнивания потенциалов КУП1 (ванная) и КУП2 (санузел 2) — высота 300 мм, у входа, вне зон 0–2, проводник от шины РЕ щита ЩК, сече; Р17 — высота 1700 мм выше нормы 1 м (ПУЭ 6.6.30) по назначению: питание слаботочного щита ЩС, рядом со щитом на его высоте.

Открытые вопросы и конфликты по листу: К-4.

См. лист открытых вопросов (лист 6, записи К-1–К-4).

Примечания

1. За отметку 0,000 принят уровень чистого пола. Высоты Н — от чистого пола до оси изделия; привязки — от чистовой грани стены до оси механизма (у рамки на несколько постов — до оси рамки).
2. Высота установки, не указанная на плане: розетки — 300 мм от чистого пола; выводы кабеля — по паспорту прибора.
3. Розетки в санузле — только вне зон 0–2 (ПУЭ 7.1.48, ГОСТ Р 50571.7.701-2024), IP44, через УЗО 30 мА.
4. Розеточные и мокрые линии — через УЗО или дифавтомат с током утечки не более 30 мА (ПУЭ 7.1.79); в санузле выполнить ДСУП (ПУЭ 7.1.87–7.1.88).
5. Кабель — медный, исполнение нг(А)-LS (ГОСТ 31565-2012); скрытая прокладка только горизонтально и вертикально, фактические трассы зафиксировать исполнительной схемой до закрытия отделкой.
6. Расчёт нагрузок, токов КЗ, селективности и сечений — по проекту ЭОМ организации с допуском СРО; лист задаёт состав, расположение и группы.
7. Выводы кухонной техники — после утверждения проекта кухни (ориентировочно); привязки выводов даны от осей модулей гарнитура и пересматриваются вместе с проектом кухни.
8. Электрический тёплый пол проектом не предусмотрен; при решении заказчика устроить — отдельный лист «План тёплых полов»: контуры с отступом 100 мм от стен и мебели без ножек, датчик в гофре, терморегулятор, своя группа щита через УЗО 30 мА.
9. Ведомости электроточек, изделий, светильников и расшифровка клавиш — лист 34.

1000 мм · печать 1:1

Изм.	Кол.уч	Лист	№ док.	Подп.	Дата
Разраб.		Кырлан А.С.			19.10.26
Пров.					
ГИП					
Н. контр.					
Утв.					

ГД-2026-012-АИ

Дом 120 м²

Общая площадь 147,36* м² · * размеры приняты, не замерены (реестр — л. 6, К-1)

Дизайн-проект интерьера

Стадия	Лист	Листов
РП	28	130

План розеток и электровыводов · 1-й этаж

М 1:50

Кырлан Александр Сергеевич

выпуск 19.10.2026 № 53e4f7ddae · стр. 31 из 160

План розеток и электровыводов · 2-й этаж

Розетки, выводы кабеля, щит · размеры в мм · высоты от чистого пола

ПРЕДВАРИТЕЛЬНО · не для производства работ · открыто пунктов: 6 (реестр — л. 6)

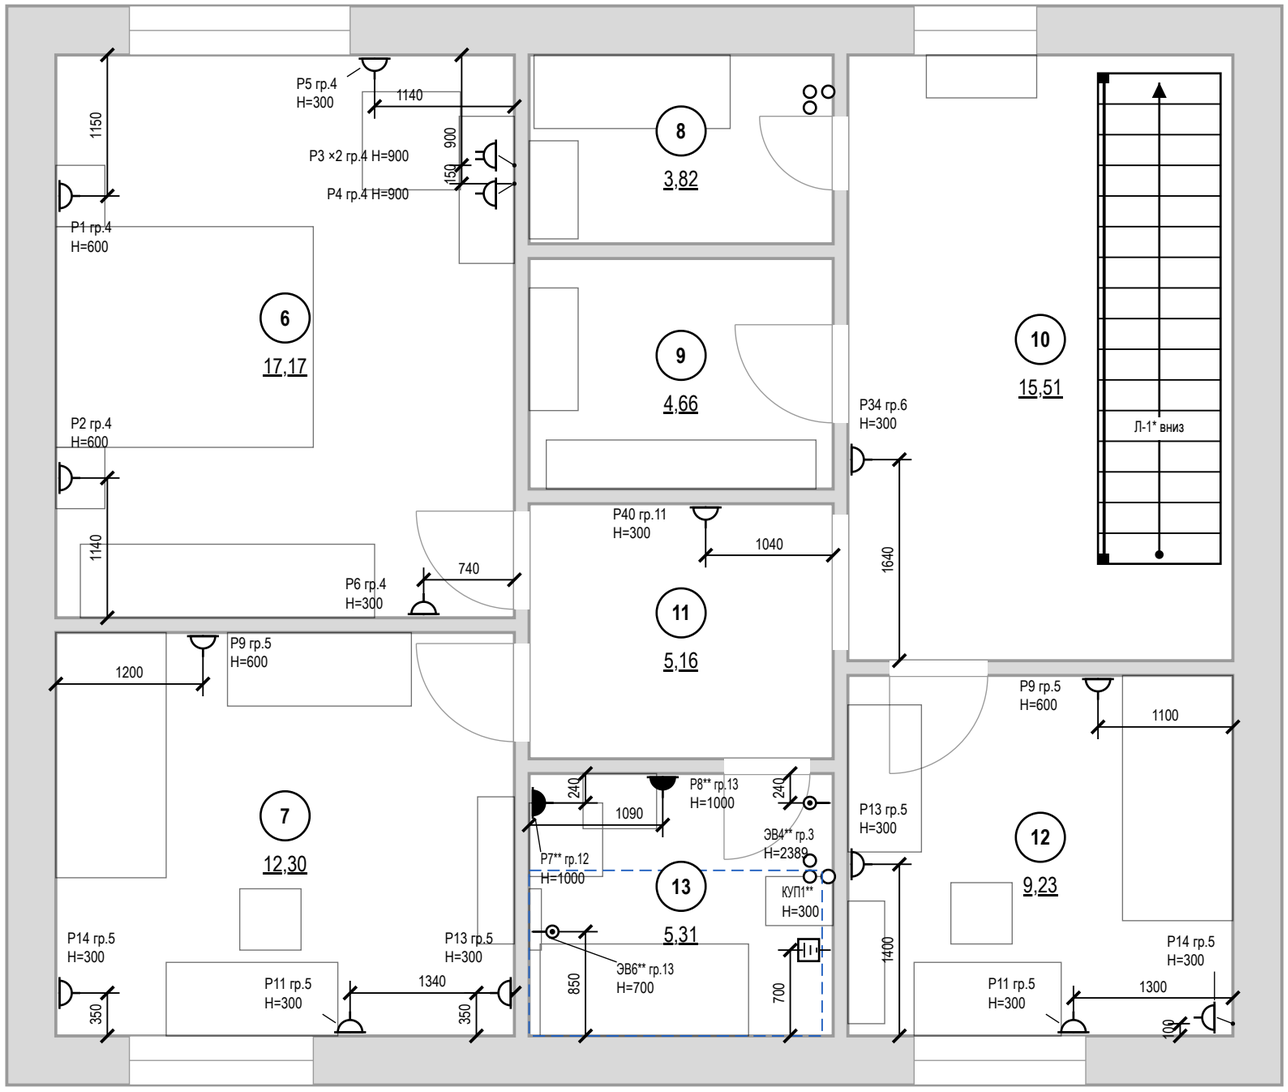

Условные обозначения

- розетка с заземляющим контактом; у знака — марка, ×N постов в рамке, гр. — группа щита, Н — высота оси, мм
- то же, рамка на 2 поста (число черточек — число постов)
- розетка влагозащищённая IP44
- вывод кабеля для подключения прибора (без розетки), марка ЭВ
- КУП — коробка уравнивания потенциалов (ДСУП), проводник к шине РЕ щита
- знак разведён для читаемости: точка на стене — у выноски, привязка — до неё
- граница зоны 2 ванной (600 мм от ванны/поддона)
- мебель и сантехприборы — подложка
- стояк: К1 — канализация, В1 — ХВС, Т3 — ГВС
- 1 — номер помещения, площадь м²

Допущения и предложения на листе

Основа листа: взаимное расположение помещений, контур дома 9600 × 8000 и раскладка этажей подобраны проектировщиком под габариты помещений брифа; обмер и проект АР — задание (К-1); высота потолка 2900 мм — по брифу, не замерена; перекрытие 330 мм и отметка 2-го этажа +3,230 приняты; проект КР — задание (К-2); наружные стены 400 мм, перегородки 120 мм приняты (в брифе толщин нет) (К-1); разрешённая мощность 15 кВт принята по типовым ТУ для частного дома (К-4).

Знак «*» — принято, не замерено и не подтверждено (замерить на объекте): К-3: Л-1 — место, тип и размеры лестницы брифом не заданы (только «лестница из холла 1-го этажа»): одномаршевая 17 × 190 × 250 вдоль стены Б холла — предложение проектировщика; конструкция и расчёт — проект КР.

Знак «**» — предложение проектировщика, заказчиком не утверждено (согласовать с заказчиком): записи в реестре нет: Р7, Р8 — по образцу: Р7, Р8 и Р33 на высоте 1000 мм — верхний предел нормы (ПУЭ, п. 6.6.30, не выше 1 м); флаг решения снят; ЭВ4, КУП1 — по образцу: Добавлены выводы к вентиляторам: ЭВ4 (ВР1, ванная) и ЭВ5 (ВР3, санузел 2) — группа 3, высота 2389 мм, включение с основным светом, таймер выбега в вентиляторе; и коробки уравнивания потенциалов КУП1 (ванная) и КУП2 (санузел 2) — высота 300 мм, у входа, вне зон 0–2, проводник от шины РЕ щита ЩК, сече; ЭВ6 — по образцу: Добавлены электрические полотенцесушители IP44: П10 в ванной (480 мм, низ 900 мм) и П13 в санузле 2 (400 мм, низ 900 мм), выводы ЭВ6 и ЭВ7; мощность группы 13 — 2,4 кВт вместо 1,8 кВт.

Открытые вопросы и конфликты по листу: К-4.

См. лист открытых вопросов (лист 6, записи К-1–К-4).

Примечания

1. За отметку 0,000 принят уровень чистого пола. Высоты Н — от чистого пола до оси изделия; привязки — от чистовой грани стены до оси механизма (у рамки на несколько постов — до оси рамки).
2. Высота установки, не указанная на плане: розетки — 300 мм от чистого пола; выводы кабеля — по паспорту прибора.
3. Розетки в санузле — только вне зон 0–2 (ПУЭ 7.1.48, ГОСТ Р 50571.7.701-2024), IP44, через УЗО 30 мА.
4. Розеточные и мокрые линии — через УЗО или дифавтомат с током утечки не более 30 мА (ПУЭ 7.1.79); в санузле выполнить ДСУП (ПУЭ 7.1.87–7.1.88).
5. Кабель — медный, исполнение нг(А)-LS (ГОСТ 31565-2012); скрытая прокладка только горизонтально и вертикально, фактические трассы зафиксировать исполнительной схемой до закрытия отделкой.
6. Расчёт нагрузок, токов КЗ, селективности и сечений — по проекту ЭОМ организации с допуском СРО; лист задаёт состав, расположение и группы.
7. Электрический тёплый пол проектом не предусмотрен; при решении заказчика устроить — отдельный лист «План тёплых полов»: контуры с отступом 100 мм от стен и мебели без ножек, датчик в гофре, терморегулятор, своя группа щита через УЗО 30 мА.
8. Ведомости электроточек, изделий, светильников и расшифровка клавиш — лист 34.

1000 мм · печать 1:1

Изм.	Кол.уч	Лист	№ док.	Подп.	Дата
Разраб.		Кырлан А.С.			19.10.26
Пров.					
ГИП					
Н. контр.					
Утв.					

ГД-2026-012-АИ

Дом 120 м²

Общая площадь 147,36* м² · * размеры приняты, не замерены (реестр — л. 6, К-1)

Дизайн-проект интерьера

Стадия	Лист	Листов
РП	29	130

План розеток и электровыводов · 2-й этаж

М 1:50

Кырлан Александр Сергеевич

выпуск 19.10.2026 № 53e4f7ddae · стр. 32 из 160

План освещения · 1-й этаж

Светильники, группы включения, извещатели · размеры в мм

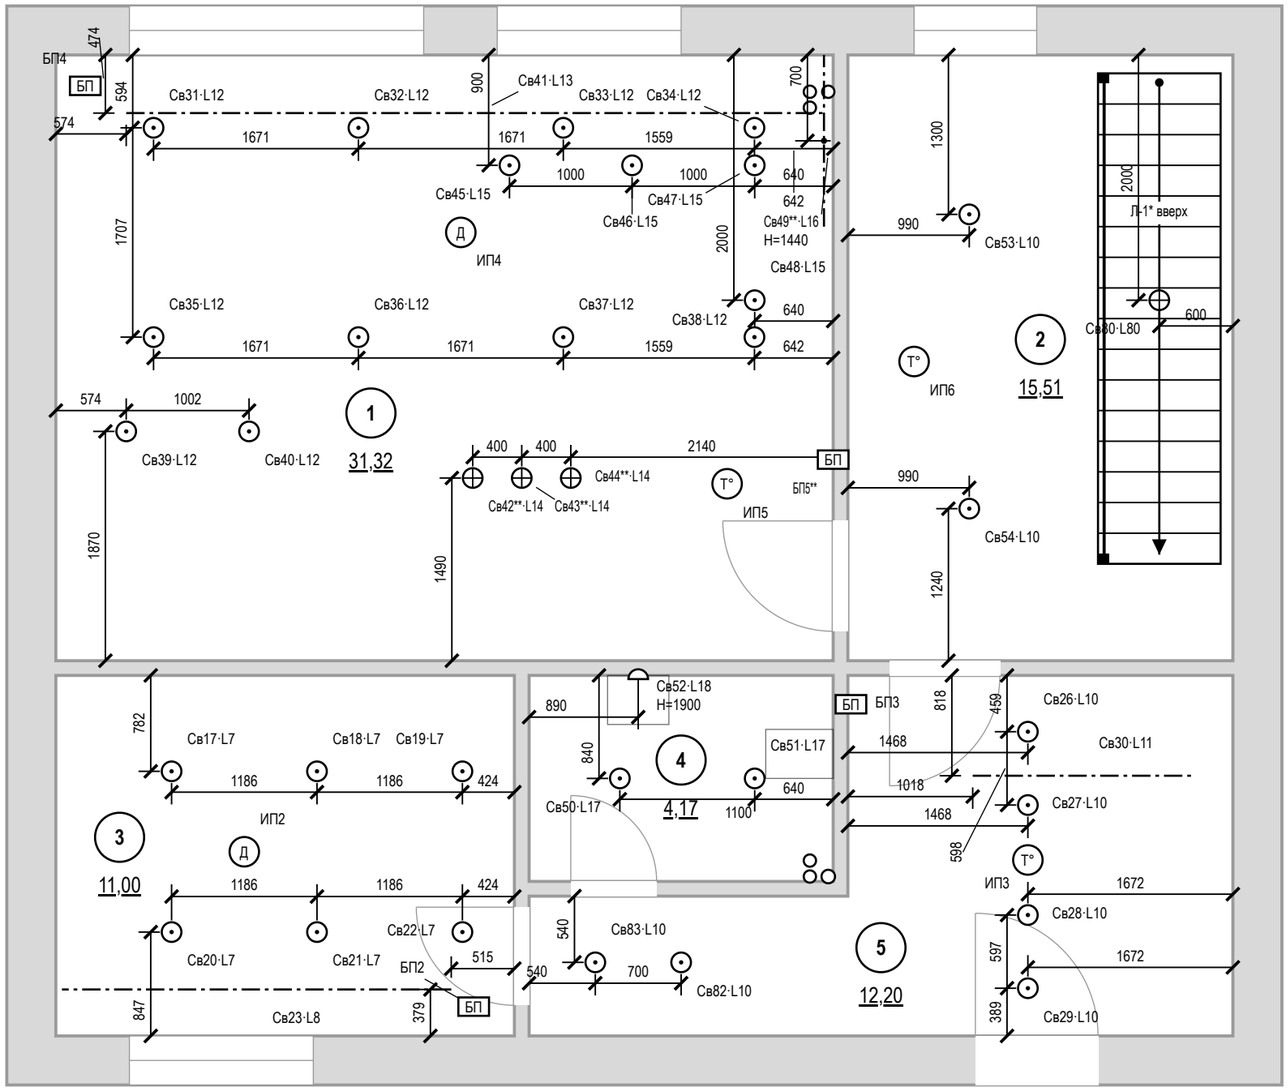

Условные обозначения

- светильник встраиваемый точечный
- светильник подвесной
- светильник настенный (бра), H — высота оси
- линейный светильник настенный (подсветка столешницы), точка — вывод питания
- светодиодная лента в профиле / в карнизе короба
- Св1·L1 — марка светильника (как в ведомости и на развёртках) · группа включения L (лист выключателей)
- Д — извещатель пожарный дымовой автономный
- Т° — извещатель пожарный тепловой
- БП — блок питания LED, с доступом (люк от 100×100 мм)
- 1 — номер помещения, площадь м²

Освещённость (оценка)

Пом.	S, м²	Ен, лк	Ф треб., лм	Ф по пр., лм
1	31,3	150	13230	16000
2	15,5	50	2180	2300
3	11	300	9300	8400
4	4,2	50	590	1100
5	12,2	50	1720	3600

Допущения и предложения на листе

Основа листа: взаимное расположение помещений, контур дома 9600 × 8000 и раскладка этажей подобраны проектировщиком под габариты помещений брифа; обмер и проект АР — задание (К-1); высота потолка 2900 мм — по брифу, не замерена; перекрытие 330 мм и отметка 2-го этажа +3,230 приняты; проект КР — задание (К-2); наружные стены 400 мм, перегородки 120 мм приняты (в брифе толщин нет) (К-1); разрешённая мощность 15 кВт принята по типовым ТУ для частного дома (К-4).

Знак «*» — принято, не замерено и не подтверждено (замерить на объекте): К-3: Л-1 — место, тип и размеры лестницы брифом не заданы (только «лестница из холла 1-го этажа»): одномаршевая 17 × 190 × 250 вдоль стены Б холла — предложение проектировщика; конструкция и расчёт — проект КР.

Знак «**» — предложение проектировщика, заказчиком не утверждено (согласовать с заказчиком): записи в реестре нет: Св42, Св43, Св44, Св49, БП5 — диммируемость добавлена разработчиком проекта под светорегуляторы S11 и S12.

См. лист открытых вопросов (лист 6, записи К-1–К-4).

Примечания

1. За отметку 0,000 принят уровень чистого пола. Высоты H — от чистого пола до оси изделия; привязки — от чистовой грани стены до оси механизма (у рамки на несколько постов — до оси рамки).
2. Высота установки, не указанная на плане: светильники — на потолке; настенные — по отметке H у знака. Привязки — до оси светильника от чистовой грани стены, по рядам.
3. Освещённость: Ен — СанПиН 1.2.3685-21, табл. 5.52 (на полу); Ф треб. = Ен·S/(U·MF) при U = 0,5 и MF = 0,71 (СП 52.13330.2016, табл. 4.3) — оценка, не светотехнический расчёт. Декоративная подсветка в Ф не входит.
4. Во влажных помещениях — светильники не ниже IP44; в зонах 0–2 ванной — по ГОСТ Р 50571.7.701-2024 (зона 1 — IPX5).
5. Розеточные и мокрые линии — через УЗО или дифавтомат с током утечки не более 30 мА (ПУЭ 7.1.79); в санузле выполнить ДСУП (ПУЭ 7.1.87–7.1.88).
6. Кабель — медный, исполнение нг(A)-LS (ГОСТ 31565-2012); скрытая прокладка только горизонтально и вертикально, фактические трассы зафиксировать исполнительной схемой до закрытия отделкой.
7. Расчёт нагрузок, токов КЗ, селективности и сечений — по проекту ЭОМ организации с допуском СРО; лист задаёт состав, расположение и группы.
8. Ведомость светильников — лист 34.

1000 мм · печать 1:1

Изм.	Кол.уч	Лист	№ док.	Подп.	Дата
Разраб.		Кырлан А.С.			19.10.26
Пров.					
ГИП					
Н. контр.					
Утв.					

ГД-2026-012-АИ

Дом 120 м²

Общая площадь 147,36* м² · * размеры приняты, не замерены (реестр — л. 6, К-1)

Дизайн-проект интерьера

Стадия	Лист	Листов
РП	30	130

План освещения · 1-й этаж

М 1:50

Кырлан Александр Сергеевич

выпуск 19.10.2026 № 53e4f7ddae · стр. 33 из 160

План освещения · 2-й этаж

Светильники, группы включения, извещатели · размеры в мм

ПРЕДВАРИТЕЛЬНО · не для производства работ · открыто пунктов: 6 (реестр — л. 6)

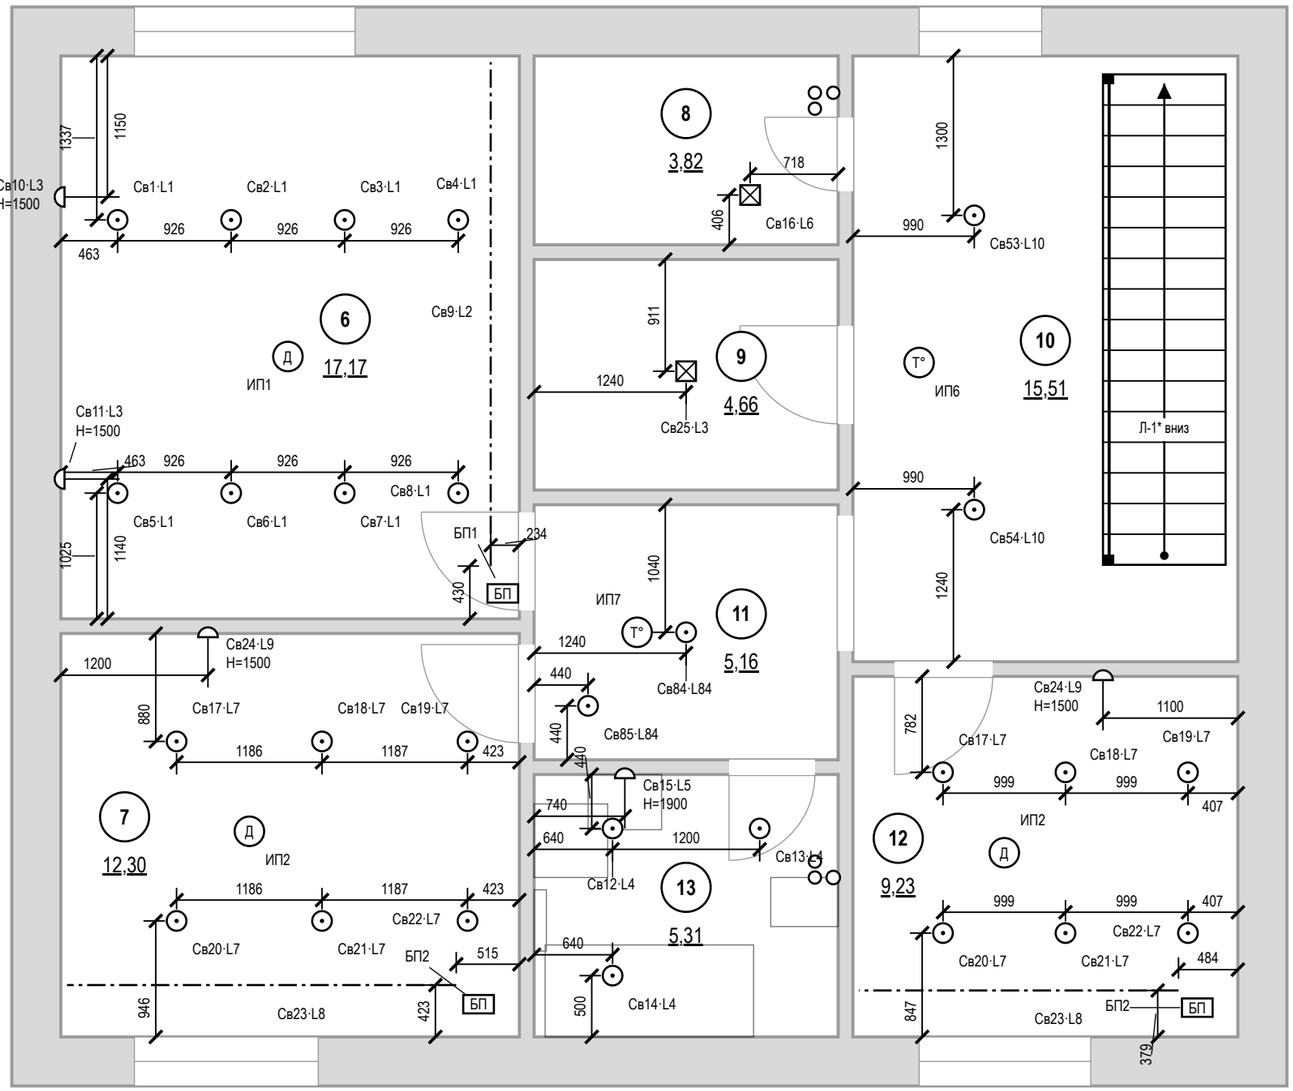

Условные обозначения

- светильник встраиваемый точечный
- светильник потолочный накладной
- светильник настенный (бра), H — высота оси
- светодиодная лента в профиле / в карнизе короба
- Св1·L1 — марка светильника (как в ведомости и на развёртках) · группа включения L (лист выключателей)
- Д — извещатель пожарный дымовой автономный
- Т° — извещатель пожарный тепловой
- БП — блок питания LED, с доступом (люк от 100×100 мм)
- 1 — номер помещения, площадь м²

Освещённость (оценка)

Пом.	S, м²	Ен, лк	Ф треб., лм	Ф по пр., лм
6	17,2	150	7250	8000
7	12,3	200	6930	6600
8	3,8	75	810	900
9	4,7	30	390	600
10	15,5	50	2180	1200
11	5,2	50	730	1200
12	9,2	200	5200	6600
13	5,3	50	750	1500

Допущения и предложения на листе

Основа листа: взаимное расположение помещений, контур дома 9600 × 8000 и раскладка этажей подобраны проектировщиком под габариты помещений брифа; обмер и проект АР — задание (К-1); высота потолка 2900 мм — по брифу, не замерена; перекрытие 330 мм и отметка 2-го этажа +3,230 приняты; проект КР — задание (К-2); наружные стены 400 мм, перегородки 120 мм приняты (в брифе толщин нет) (К-1); разрешённая мощность 15 кВт принята по типовым ТУ для частного дома (К-4).

Знак «*» — принято, не замерено и не подтверждено (замерить на объекте): К-3: Л-1 — место, тип и размеры лестницы брифом не заданы (только «лестница из холла 1-го этажа»): одномаршевая 17 × 190 × 250 вдоль стены Б холла — предложение проектировщика; конструкция и расчёт — проект КР.

См. лист открытых вопросов (лист 6, записи К-1–К-4).

Примечания

1. За отметку 0,000 принят уровень чистого пола. Высоты H — от чистого пола до оси изделия; привязки — от чистовой грани стены до оси механизма (у рамки на несколько постов — до оси рамки).
2. Высота установки, не указанная на плане: светильники — на потолке; настенные — по отметке H у знака. Привязки — до оси светильника от чистовой грани стены, по рядам.
3. Освещённость: Ен — СанПиН 1.2.3685-21, табл. 5.52 (на полу); Ф треб. = Ен·S/(U·MF) при U = 0,5 и MF = 0,71 (СП 52.13330.2016, табл. 4.3) — оценка, не светотехнический расчёт. Декоративная подсветка в Ф не входит.
4. Во влажных помещениях — светильники не ниже IP44; в зонах 0–2 ванной — по ГОСТ Р 50571.7.701-2024 (зона 1 — IPX5).
5. Розеточные и мокрые линии — через УЗО или дифавтомат с током утечки не более 30 мА (ПУЭ 7.1.79); в санузле выполнить ДСУП (ПУЭ 7.1.87–7.1.88).
6. Кабель — медный, исполнение нг(A)-LS (ГОСТ 31565-2012); скрытая прокладка только горизонтально и вертикально, фактические трассы зафиксировать исполнительной схемой до закрытия отделкой.
7. Расчёт нагрузок, токов КЗ, селективности и сечений — по проекту ЭОМ организации с допуском СРО; лист задаёт состав, расположение и группы.
8. Ведомость светильников — лист 34.

1000 мм · печать 1:1

Изм.	Кол.уч	Лист	№ док.	Подп.	Дата
Разраб.		Кырлан А.С.			19.10.26
Пров.					
ГИП					
Н. контр.					
Утв.					

ГД-2026-012-АИ

Дом 120 м²

Общая площадь 147,36* м² · * размеры приняты, не замерены (реестр — л. 6, К-1)

Дизайн-проект интерьера

Стадия	Лист	Листов
РП	31	130

План освещения · 2-й этаж

М 1:50

Кырлан Александр Сергеевич

выпуск 19.10.2026 № 53e4f7ddae · стр. 34 из 160

План выключателей и схема включения · 1-й этаж

Выключатели S, группы включения L, линии связи · размеры в мм

ПРЕДВАРИТЕЛЬНО · не для производства работ · открыто пунктов: 6 (реестр — л. 6)

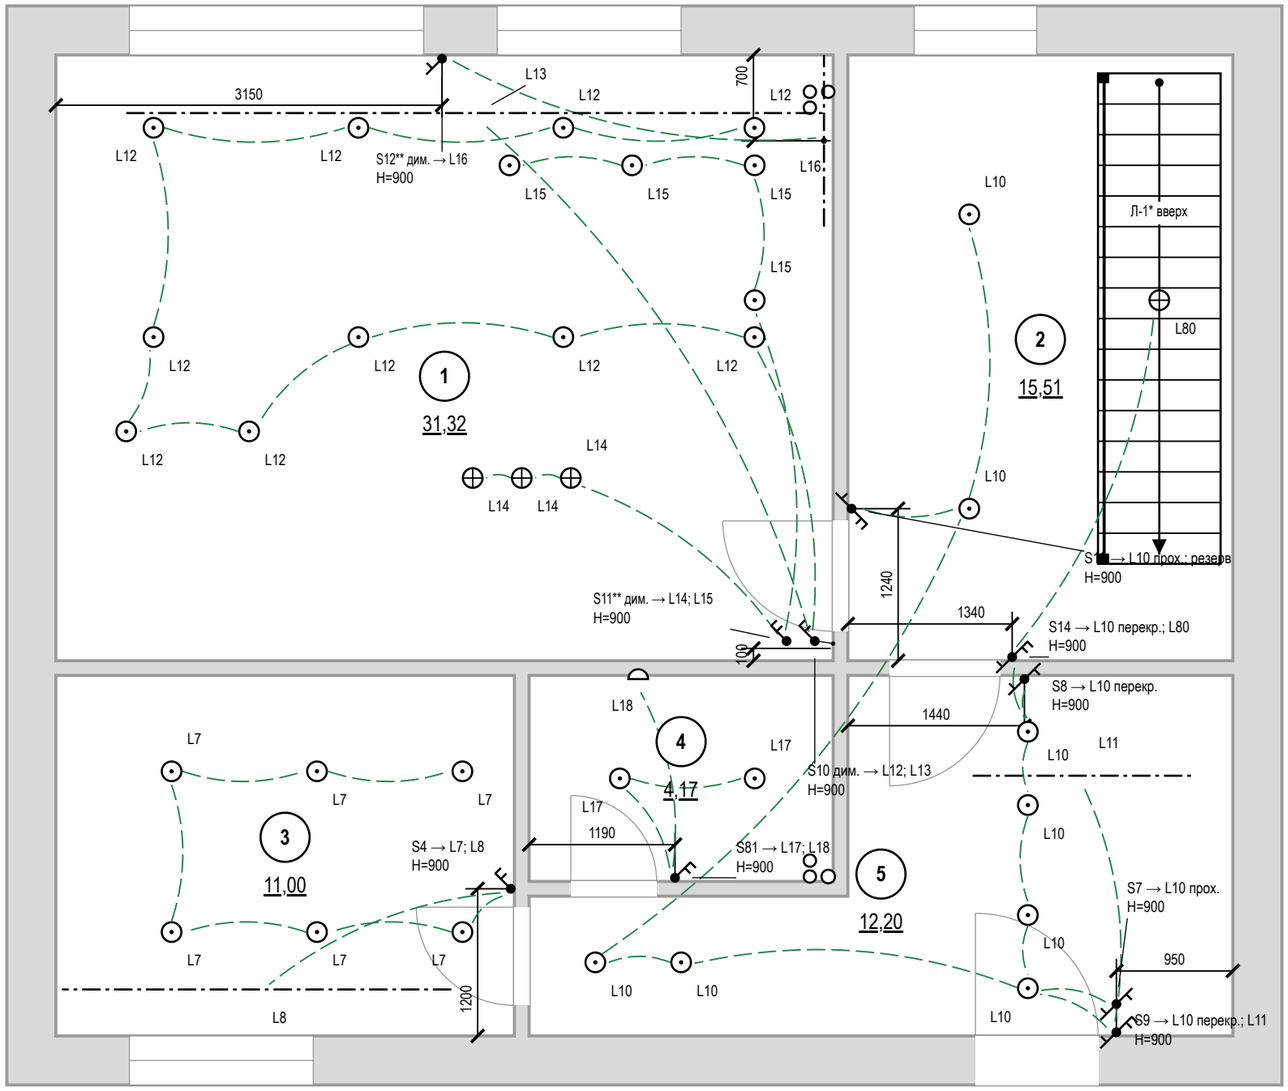

Условные обозначения

- выключатель одноклавишный
- выключатель двухклавишный (флажков — по числу клавиш)
- выключатель с проходной или перекрёстной клавишей (обратный флажок); тип клавиши — в подписи
- S1 → — марка → группы по клавишам (через «;»): прох. — проходной, перекр. — перекрёстный, дим. — светорегулятор; H — высота
- линия связи: выключатель → светильники группы (не трасса кабеля)
- светильник встраиваемый точечный
- светильник подвесной
- светильник настенный (бра), H — высота оси
- линейный светильник настенный (подсветка столешницы), точка — вывод питания
- светодиодная лента в профиле / в карнизе короба
- L1 — группа включения у светильника
- (1) — номер помещения, площадь м²

Допущения и предложения на листе

Основа листа: взаимное расположение помещений, контур дома 9600 × 8000 и раскладка этажей подобраны проектировщиком под габариты помещений брифа; обмер и проект АР — задание (К-1); высота потолка 2900 мм — по брифу, не замерена; перекрытие 330 мм и отметка 2-го этажа +3,230 приняты; проект КР — задание (К-2); наружные стены 400 мм, перегородки 120 мм приняты (в брифе толщин нет) (К-1); разрешённая мощность 15 кВт принята по типовым ТУ для частного дома (К-4).

Знак «*» — принято, не замерено и не подтверждено (замерить на объекте): К-3: Л-1 — место, тип и размеры лестницы брифом не заданы (только «лестница из холла 1-го этажа»): одномаршевая 17 × 190 × 250 вдоль стены Б холла — предложение проектировщика; конструкция и расчёт — проект КР.

Знак «**» — предложение проектировщика, заказчиком не утверждено (согласовать с заказчиком): записи в реестре нет: S11, S12 — светорегулятор добавлен разработчиком проекта.

См. лист открытых вопросов (лист 6, записи К-1–К-4).

Примечания

1. За отметку 0,000 принят уровень чистого пола. Высоты H — от чистого пола до оси изделия; привязки — от чистовой грани стены до оси механизма (у рамки на несколько постов — до оси рамки).
2. Высота установки, не указанная на плане: выключатели — 900 мм от чистого пола, со стороны дверной ручки (ПУЭ 7.1.51).
3. Линии связи показывают, какой выключатель какую группу L включает; это не трасса кабеля. Трасса — принципиальная, фактическую зафиксировать исполнительной схемой.
4. Группы из нескольких мест (L10 — S7, S8, S9, S14, S16): на крайних местах — проходные клавиши, на промежуточных — перекрёстные; механизмы — в ведомости изделий.
5. Светорегулятор — по заднему фронту (для LED-драйверов), совместимость с драйверами проверить до закупки.
6. Розеточные и мокрые линии — через УЗО или дифавтомат с током утечки не более 30 мА (ПУЭ 7.1.79); в санузле выполнить ДСУП (ПУЭ 7.1.87–7.1.88).
7. Кабель — медный, исполнение нг(A)-LS (ГОСТ 31565-2012); скрытая прокладка только горизонтально и вертикально, фактические трассы зафиксировать исполнительной схемой до закрытия отделкой.
8. Расчёт нагрузок, токов КЗ, селективности и сечений — по проекту ЭОМ организации с допуском СРО; лист задаёт состав, расположение и группы.
9. Расшифровка клавиш и ведомость изделий — лист 34.

1000 мм · печать 1:1

						ГД-2026-012-АИ	
						Дом 120 м²	
						Общая площадь 147,36* м² · * размеры приняты, не замерены (реестр — л. 6, К-1)	
Изм.	Кол.уч	Лист	№ док.	Подп.	Дата	Дизайн-проект интерьера	Стадия: РП; Лист: 32; Листов: 130
Разраб.		Кырлан А.С.			19.10.26		
Пров.							
ГИП							
Н. контр.						**План выключателей и схема включения · 1-й этаж** М 1:50	**Кырлан Александр Сергеевич**
Утв.							

выпуск 19.10.2026 № 53e4f7ddae · стр. 35 из 160

План выключателей и схема включения · 2-й этаж

Выключатели S, группы включения L, линии связи · размеры в мм

ПРЕДВАРИТЕЛЬНО · не для производства работ · открыто пунктов: 6 (реестр — л. 6)

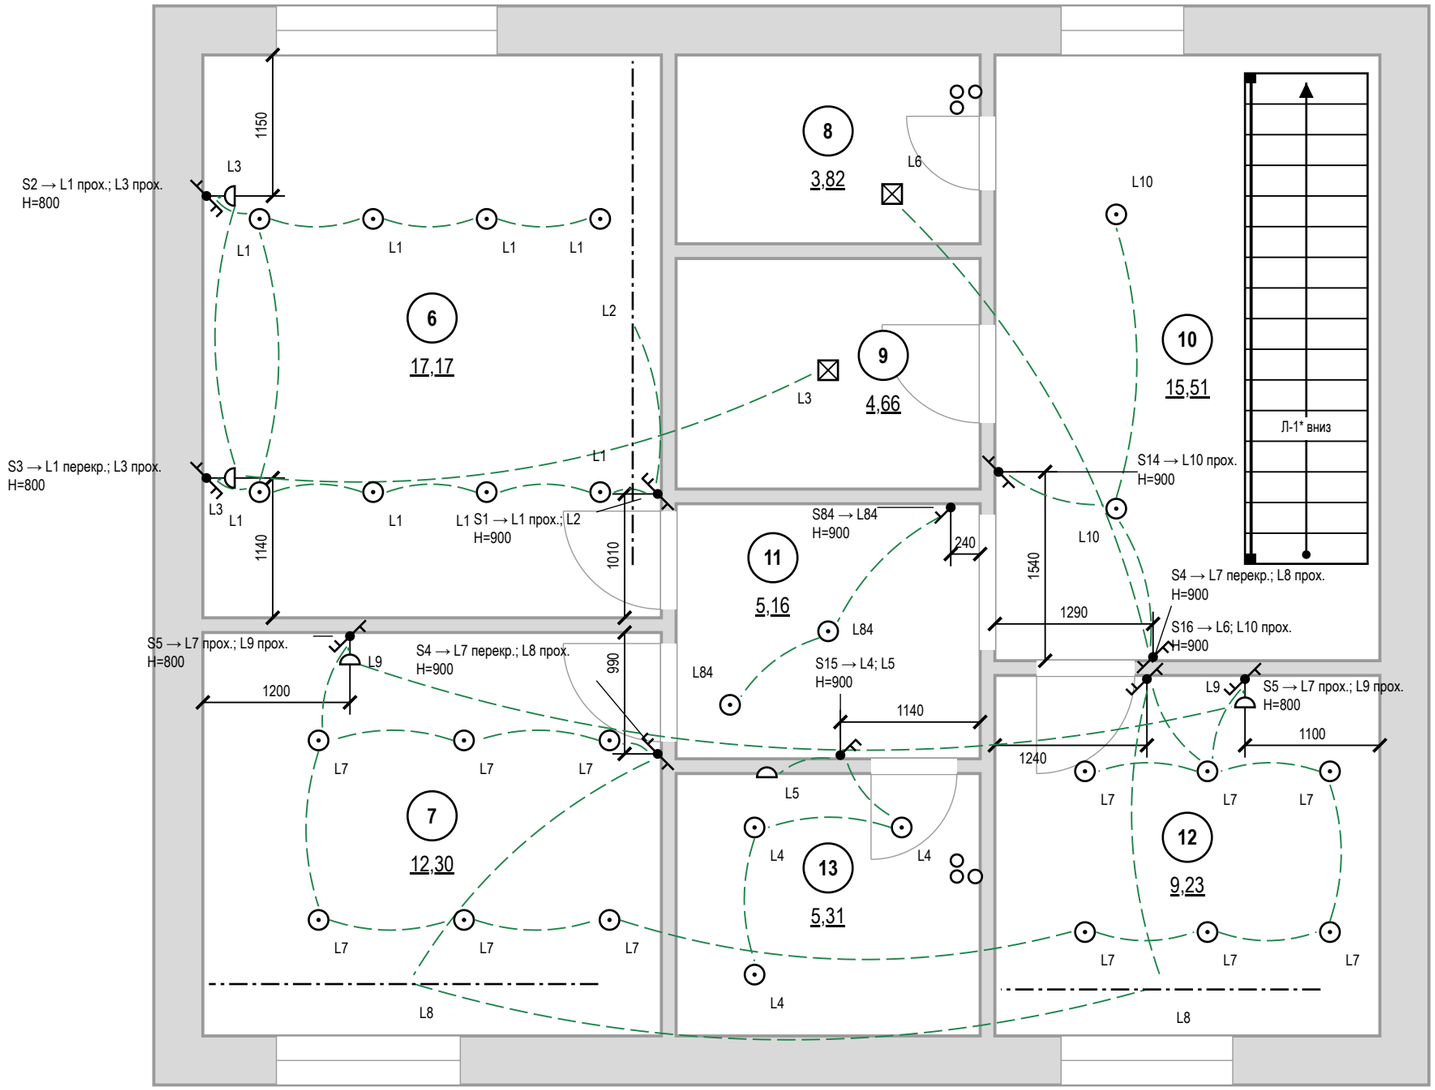

Условные обозначения

- выключатель одноклавишный
- выключатель двухклавишный (флажков — по числу клавиш)
- выключатель с проходной или перекрёстной клавишей (обратный флажок); тип клавиши — в подписи
- S1 → — марка → группы по клавишам (через «;»): прох. — проходной, перекр. — перекрёстный, дим. — светорегулятор; Н — высота
- линия связи: выключатель → светильники группы (не трасса кабеля)
- светильник встраиваемый точечный
- светильник потолочный накладной
- светильник настенный (бра), Н — высота оси
- светодиодная лента в профиле / в карнизе короба
- L1 — группа включения у светильника
- 1 — номер помещения, площадь м²

Допущения и предложения на листе

Основа листа: взаимное расположение помещений, контур дома 9600 × 8000 и раскладка этажей подобраны проектировщиком под габариты помещений брифа; обмер и проект АР — задание (К-1); высота потолка 2900 мм — по брифу, не замерена; перекрытие 330 мм и отметка 2-го этажа +3,230 приняты; проект КР — задание (К-2); наружные стены 400 мм, перегородки 120 мм приняты (в брифе толщин нет) (К-1); разрешённая мощность 15 кВт принята по типовым ТУ для частного дома (К-4).

Знак «*» — принято, не замерено и не подтверждено (замерить на объекте): К-3: Л-1 — место, тип и размеры лестницы брифом не заданы (только «лестница из холла 1-го этажа»): одномаршевая 17 × 190 × 250 вдоль стены Б холла — предложение проектировщика; конструкция и расчёт — проект КР.

См. лист открытых вопросов (лист 6, записи К-1–К-4).

Примечания

1. За отметку 0,000 принят уровень чистого пола. Высоты Н — от чистого пола до оси изделия; привязки — от чистовой грани стены до оси механизма (у рамки на несколько постов — до оси рамки).
2. Высота установки, не указанная на плане: выключатели — 900 мм от чистого пола, со стороны дверной ручки (ПУЭ 7.1.51).
3. Линии связи показывают, какой выключатель какую группу L включает; это не трасса кабеля. Трасса — принципиальная, фактическую зафиксировать исполнительной схемой.
4. Группы из нескольких мест (L1 — S1, S2, S3; L3 — S2, S3; L7 — S4, S4, S5, S5; L8 — S4, S4; L9 — S5, S5; L10 — S14, S16): на крайних местах — проходные клавиши, на промежуточных — перекрёстные; механизмы — в ведомости изделий.
5. Розеточные и мокрые линии — через УЗО или дифавтомат с током утечки не более 30 мА (ПУЭ 7.1.79); в санузле выполнить ДСУП (ПУЭ 7.1.87–7.1.88).
6. Кабель — медный, исполнение нг(А)-LS (ГОСТ 31565-2012); скрытая прокладка только горизонтально и вертикально, фактические трассы зафиксировать исполнительной схемой до закрытия отделкой.
7. Расчёт нагрузок, токов КЗ, селективности и сечений — по проекту ЭОМ организации с допуском СРО; лист задаёт состав, расположение и группы.
8. Расшифровка клавиш и ведомость изделий — лист 34.

1000 мм · печать 1:1

Изм.	Кол.уч	Лист	№ док.	Подп.	Дата
Разраб.		Кырлан А.С.			19.10.26
Пров.					
ГИП					
Н. контр.					
Утв.					

ГД-2026-012-АИ

Дом 120 м²

Общая площадь 147,36* м² · * размеры приняты, не замерены (реестр — л. 6, К-1)

Дизайн-проект интерьера

Стадия	Лист	Листов
РП	33	130

План выключателей и схема включения · 2-й этаж

М 1:50

Кырлан Александр Сергеевич

выпуск 19.10.2026 № 53e4f7ddae · стр. 36 из 160

02

Электрооборудование

Кырлан Александр Сергеевич

выпуск 19.10.2026 · 53e4f7ddae · стр. 37 из 160

Ведомость электроточек и изделий

Электроточки, изделия, светильники, клавиши выключателей · б/м

Ведомость электроточек

Марка	Пом.	Назначение	Н, мм	Гр.
Р18**	1	ТВ (в одной зоне с ТВ1, LAN3)	1100	6
Р19**	1	ТВ-приставка (в одной зоне с ТВ1, LAN3)	1100	6
Р20	1	у ТВ-тумбы	300	6
Р21	1	торшер	300	6
Р22	1	у кресла	300	6
Р23	1	уборка, пылесос	300	6
Р24	1	у обеденного стола	300	6
Р25**	1	холодильник Кх9 (розетка в соседнем модуле Кх8, съёмная панель)	150	11
Р26	1	фартук	1100	7
Р27	1	фартук	1100	7
Р28	1	фартук	1100	7
Р29	1	фартук	1100	7
Р30	1	фартук между мойкой и варочной	1100	7
Р31	1	фартук между мойкой и варочной	1100	7
Р32	1	посудомоечная машина	300	10
ЭВ1	1	варочная панель (в соседнем модуле М8.3, за ящиком)	600	8
ЭВ2	1	духовой шкаф	150	9
ЭВ3	1	вытяжка	2200	11
Р34	2	уборка	300	6
Р9	3	у кровати	600	5
Р10	3	у кровати	600	5
Р11	3	у комода	300	5
Р13	3	уборка	300	5
Р14	3	уборка у входа	300	5
КУП2**	4	КУП — уравнивание потенциалов (ДСУП)	300	
Р33**	4	фен у умывальника, IP44	1000	13
ЭВ5**	4	вентилятор ВР3 (таймер выбега)	2389	3
Р15	5	пылесос, сушилка обуви	300	6
Р16	5	уборка	300	6
Р17**	5	питание слаботочного щита (рядом с ЩС**)	1700	14

Ведомость электроточек (продолжение)

Марка	Пом.	Назначение	Н, мм	Гр.
ЩК	5	щит квартирный ЩРВ-П-48	1700	
Р1	6	у кровати	600	4
Р2	6	у кровати	600	4
Р3	6	рабочий стол	900	4
Р4	6	рабочий стол	900	4
Р5	6	торшер у кресла	300	4
Р6	6	уборка	300	4
Р9	7	у кровати	600	5
Р11	7	у комода	300	5
Р13	7	уборка	300	5
Р14	7	уборка у входа	300	5
Р34	10	уборка	300	6
Р40	11	уборка	300	11
Р9	12	у кровати	600	5
Р11	12	у комода	300	5
Р13	12	уборка	300	5
Р14	12	уборка у входа	300	5
КУП1**	13	КУП — уравнивание потенциалов (ДСУП)	300	
Р7**	13	стиральная машина, IP44	1000	12
Р8**	13	фен у умывальника, IP44	1000	13
ЭВ4**	13	вентилятор ВР1 (таймер выбега)	2389	3
ЭВ6**	13	полотенцесушитель П10, IP44	700	13

Ведомость изделий

Наименование	Марки	Ед.	Кол.
Розетка с з/к и защитными шторками, 16 А	по ведомости точек	шт	45
Розетка IP44 с крышкой, 16 А	Р7**, Р8**, Р33**	шт	3
Выключатель 1-клав.	S84	шт	1
Выключатель 1-клав. перекрёстный	S8	шт	1
Выключатель 1-клав. проходной	S7, S14	шт	2
Выключатель 2-клав.	S15, S81	шт	2
Выключатель 2-клав. (перекрёстная + обычная)	S9	шт	1

Ведомость изделий (продолжение)

Наименование	Марки	Ед.	Кол.
Выключатель 2-клав. (перекрёстная + проходная)	S3, S4, S16	шт	6
Выключатель 2-клав. (проходная + обычная)	S1, S14	шт	2
Выключатель 2-клав. проходной	S2, S5	шт	3
Светорегулятор 1-канальный, задний фронт (LED)	S12**	шт	1
Светорегулятор 2-канальный, задний фронт (LED)	S10, S11**	шт	2
Датчик движения ночной подсветки	L11	шт	1
Рамка 1-постовая	в т. ч. 21 под выключ.	шт	59
Рамка 2-постовая		шт	5
Коробка установочная (подрозетник) Ø68	розетки, выключатели	шт	69
Вывод кабеля под прибор (клеммник)	ЭВ1–ЭВ3, ЭВ4**, ЭВ5**, ЭВ6**	шт	6
Коробка уравнивания потенциалов КУП	КУП1**, КУП2**	шт	2
Блок питания LED 24 В, 300 Вт, дим.	БП4	шт	1
Блок питания LED 24 В, 60 Вт, дим.	БП5**	шт	1
Блок питания LED 24 В, 200 Вт, дим.	БП1, БП2	шт	4
Блок питания LED 24 В, 20 Вт	БП3	шт	1
Извещатель дымовой автономный	ИП1, ИП2, ИП4	шт	5
Извещатель тепловой	ИП3, ИП5–ИП7	шт	5
Щит квартирный (состав — лист щита)	ЩК	шт	1
Розетка компьютерная RJ45, кат. 6, с рамкой и подрозетником	LAN2, LAN3	шт	4
Розетка телевизионная (коаксиальная) с рамкой и подрозетником	ТВ1	шт	1
Точка доступа Wi-Fi (оборудование заказчика), питание PoE	АР1**, АР2**	шт	2
Трубка или монитор домофона (поставка домофонной организации)	ДФ1	шт	1
Щит слаботочный ЩС**: корпус, DIN-рейка, розетки 220 В	ЩС**	шт	1
Патч-панель, портов не менее 6		шт	1
Коммутатор, портов не менее 6, из них PoE 2		шт	1

Ведомость изделий (продолжение)

Наименование	Марки	Ед.	Кол.
Кабель домофона — тип по системе поставщика (по лучам от ЩС**, запас 10 %)		м	6,1
Кабель коаксиальный RG-6 (75 Ом) к розеткам ТВ (по лучам от ЩС**, запас 10 %)		м	16,7
Кабель U/UTP кат. 6 (LAN, Wi-Fi и камеры по PoE) (по лучам от ЩС**, запас 10 %)		м	71

Ведомость светильников

Поз.	Марки	Тип	Кол.	Р, Вт	Ф, лм	IP	Тц/Ra
1	Св31–Св40	встраиваемый точечный	10	12	1000		3000/90
2	Св41	светодиодная лента, 22,1 м	1	212,2	19890		2700/90
3	Св42**, Св43**, Св44**	подвесной	3	9	800		3000/90
4	Св45–Св48	встраиваемый точечный	4	10	900		3000/90
5	Св49**	линейный светильник, Н=1440	1	18	1500		3000/90
6	Св26–Св29, Св53, Св54, Св82–Св85	встраиваемый точечный	12	7	600		3000/90
7	Св80	подвесной	1	12	1100		3000/90
8	Св17–Св22	встраиваемый точечный	6	14	1400		2700/90
9	Св23	светодиодная лента, 12,3 м	1	14	1400		2700/90
10	Св50	встраиваемый точечный	1	7	600	44	3000/90
11	Св12–Св14, Св51	встраиваемый точечный	4	6	500	44	3000/90
12	Св15, Св52	настенный (бра), Н=1900	2	8	600	44	3000/90
13	Св30	светодиодная лента, 1,8 м	1	8,6	270		2700/90
14	Св1–Св8	встраиваемый точечный	8	12	1000		2700/90
15	Св9	светодиодная лента, 15,5 м	1	148,8	13950		2700/90
16	Св10, Св11, Св24	настенный (бра), Н=1500	4	6	400		2700/90
17	Св17–Св22	встраиваемый точечный	12	11	1100		2700/90

Примечания

1. Ведомости сведены с планов розеток, освещения и выключателей; марки, группы и высоты — те же, что у знаков на планах.
2. Механизмы, рамки и светорегуляторы — одной серии; число постов и клавиш сверено с выбранной серией. Перекрёстная клавиша — отдельный механизм серии.
3. За отметку 0,000 принят уровень чистого пола. Высоты Н — от чистого пола до оси изделия; привязки — от чистовой грани стены до оси механизма (у рамки на несколько постов — до оси рамки).
4. Розеточные и мокрые линии — через УЗО или дифавтомат с током утечки не более 30 мА (ПУЭ 7.1.79); в санузле выполнить ДСУП (ПУЭ 7.1.87–7.1.88).
5. Кабель — медный, исполнение нг(А)-LS (ГОСТ 31565-2012); скрытая прокладка только горизонтально и вертикально, фактические трассы зафиксировать исполнительной схемой до закрытия отделкой.
6. Расчёт нагрузок, токов КЗ, селективности и сечений — по проекту ЭОМ организации с допуском СРО; лист задаёт состав, расположение и группы.
7. Ведомости занимают 2 листов этого наименования: таблицы, не вошедшие в поле листа, продолжены на следующем листе.

Допущения и предложения на листе. Знак «**» предложено (согласовать). См. лист открытых вопросов (лист 6).

Изм.	Кол.уч	Лист	№ док.	Подп.	Дата
Разраб.		Кырлан А.С.			19.10.26
Пров.					
ГИП					
Н. контр.					
Утв.					

ГД-2026-012-АИ

Дом 120 м²

Общая площадь 147,36* м² · * размеры приняты, не замерены (реестр — л. 6, К-1)

Дизайн-проект интерьера

Стадия	Лист	Листов
РП	34	130

Ведомость электроточек и изделий

М б/м

Кырлан Александр Сергеевич

Ведомость электроточек и изделий (продолжение)

Электроточки, изделия, светильники, клавиши выключателей · б/м

Ведомость светильников (продолжение)

Поз.	Марки	Тип	Кол.	P, Вт	Ф, лм	IP	Тц/Ra
18	Св23	светодиодная лента, 12,3 м	2	11	1100		2700/90
19	Св16	потолочный накладной	1	10	900		3000/90
20	Св25	потолочный накладной	1	9	600		3000/90

Расшифровка клавиш

Марка	Пом.	H, мм	Клав.	Механизм	Группа: светильники
S1	6	900	1	проходной	L1: Св1–Св8
			2	обычный	L2: Св9
S2	6	800	1	проходной	L1: Св1–Св8
			2	проходной	L3: Св10, Св11, Св25
S3	6	800	1	перекрёстный	L1: Св1–Св8
			2	проходной	L3: Св10, Св11, Св25
S4	3	900	1	перекрёстный	L7: Св17–Св22
			2	проходной	L8: Св23
S4	7	900	1	перекрёстный	L7: Св17–Св22
			2	проходной	L8: Св23
S4	12	900	1	перекрёстный	L7: Св17–Св22
			2	проходной	L8: Св23
S5	7	800	1	проходной	L7: Св17–Св22
			2	проходной	L9: Св24
S5	12	800	1	проходной	L7: Св17–Св22
			2	проходной	L9: Св24
S7	5	900	1	проходной	L10: Св26–Св29, Св53, Св54, Св82, Св83
S8	5	900	1	перекрёстный	L10: Св26–Св29, Св53, Св54, Св82, Св83
S9	5	900	1	перекрёстный	L10: Св26–Св29, Св53, Св54, Св82, Св83
			2	обычный	L11: Св30
S10	1	900	1	светорегулятор	L12: Св31–Св40
			2	светорегулятор	L13: Св41
S11**	1	900	1	светорегулятор	L14: Св42**, Св43**, Св44**
			2	светорегулятор	L15: Св45–Св48

Расшифровка клавиш (продолжение)

Марка	Пом.	H, мм	Клав.	Механизм	Группа: светильники
S12**	1	900	1	светорегулятор	L16: Св49**
S14	2	900	1	проходной	L10: Св26–Св29, Св53, Св54, Св82, Св83
			2	обычный	L80: Св80
S14	10	900	1	проходной	L10: Св26–Св29, Св53, Св54, Св82, Св83
S15	11	900	1	обычный	L4: Св12–Св14
			2	обычный	L5: Св15
S16	2	900	1	проходной	L6: Св16
			2	перекрёстный	L10: Св26–Св29, Св53, Св54, Св82, Св83
S16	10	900	1	проходной	L6: Св16
			2	перекрёстный	L10: Св26–Св29, Св53, Св54, Св82, Св83
S81	4	900	1	обычный	L17: Св50, Св51
			2	обычный	L18: Св52
S84	11	900	1	обычный	L84: Св84, Св85

Допущения и предложения на листе

Основа листа: взаимное расположение помещений, контур дома 9600 × 8000 и раскладка этажей подобраны проектировщиком под габариты помещений брифа; обмер и проект АР — задание (К-1); высота потолка 2900 мм — по брифу, не замерена; перекрытие 330 мм и отметка 2-го этажа +3,230 приняты; проект КР — задание (К-2); наружные стены 400 мм, перегородки 120 мм приняты (в брифе толщин нет) (К-1); разрешённая мощность 15 кВт принята по типовым ТУ для частного дома (К-4).

Знак «**» — предложение проектировщика, заказчиком не утверждено (согласовать с заказчиком): записи в реестре нет: S11, S12 — светорегулятор добавлен разработчиком проекта; Св42, Св43, Св44, Св49 — диммируемость добавлена разработчиком проекта под светорегуляторы S11 и S12.

См. лист открытых вопросов (лист 6, записи К-1, К-2, К-4).

Примечания

1. Продолжение ведомостей: лист 2 из 2 этого наименования; таблицы, прерванные на предыдущем листе, продолжены с заголовком «(продолжение)».
2. За отметку 0,000 принят уровень чистого пола. Высоты H — от чистого пола до оси изделия; привязки — от чистовой грани стены до оси механизма (у рамки на несколько постов — до оси рамки).
3. Розеточные и мокрые линии — через УЗО или дифавтомат с током утечки не более 30 мА (ПУЭ 7.1.79); в санузле выполнить ДСУП (ПУЭ 7.1.87–7.1.88).
4. Кабель — медный, исполнение нг(A)-LS (ГОСТ 31565-2012); скрытая прокладка только горизонтально и вертикально, фактические трассы зафиксировать исполнительной схемой до закрытия отделкой.
5. Расчёт нагрузок, токов КЗ, селективности и сечений — по проекту ЭОМ организации с допуском СРО; лист задаёт состав, расположение и группы.

Изм.	Кол.уч	Лист	№ док.	Подп.	Дата
Разраб.		Кырлан А.С.			19.10.26
Пров.					
ГИП					
Н. контр.					
Утв.					

ГД-2026-012-АИ

Дом 120 м²

Общая площадь 147,36* м² · * размеры приняты, не замерены (реестр — л. 6, К-1)

Дизайн-проект интерьера

Стадия	Лист	Листов
РП	35	130

Ведомость электроточек и изделий (продолжение)

М б/м

Кырлан Александр Сергеевич

выпуск 19.10.2026 № 53e4f7ddae · стр. 39 из 160

Однолинейная схема щита

Щит квартирный ЩК · гр. 1—9 из 17 · без масштаба

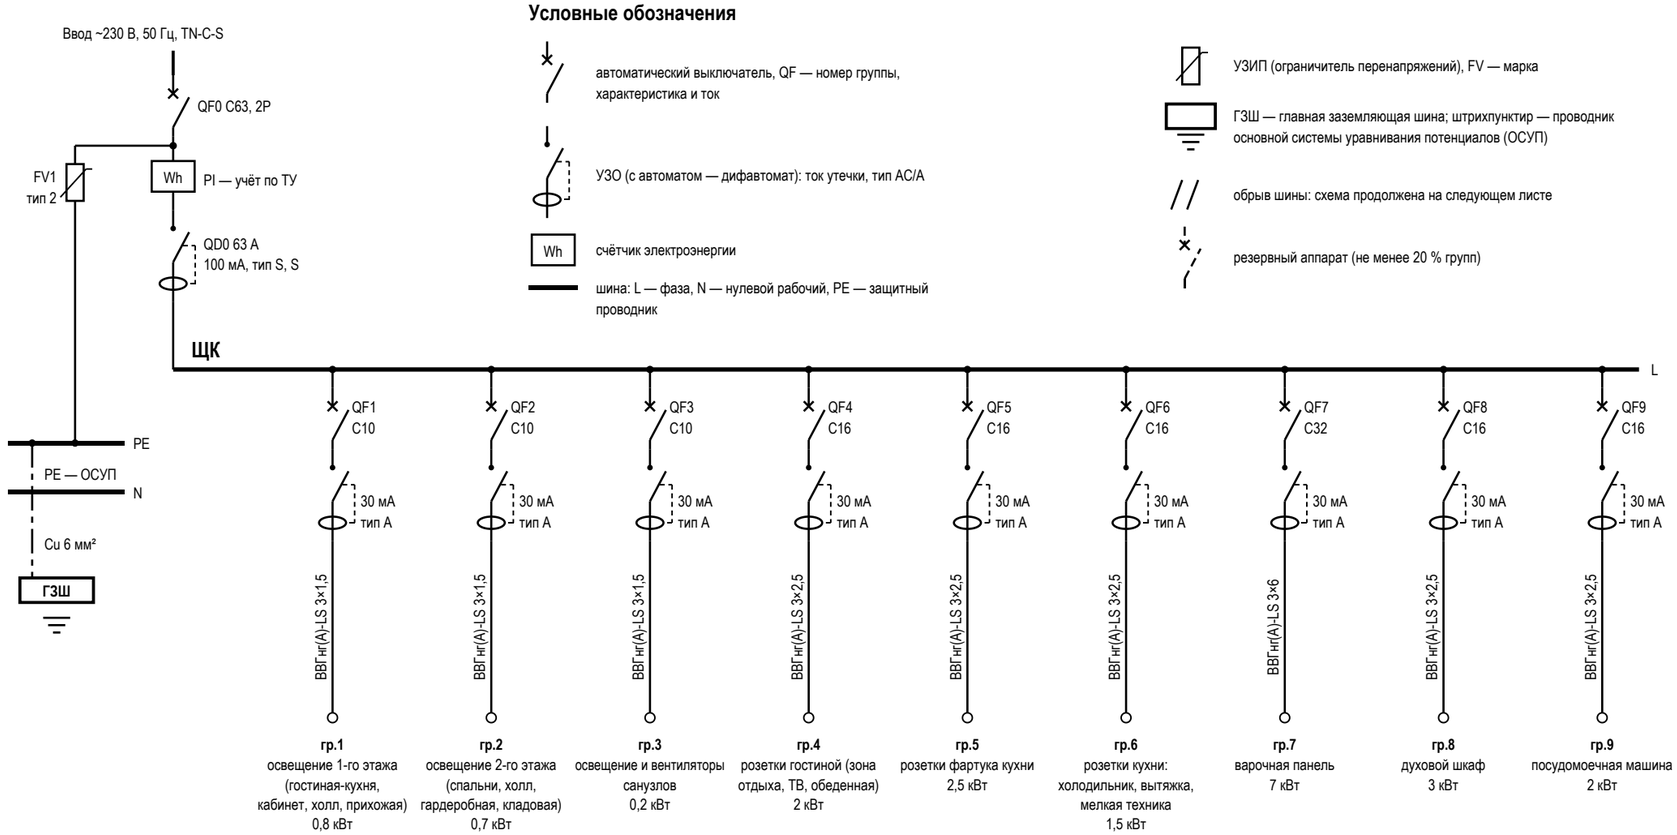

Условные обозначения

- автоматический выключатель, QF — номер группы, характеристика и ток
- УЗО (с автоматом — дифавтомат): ток утечки, тип AC/A
- Wh — счётчик электроэнергии
- шина: L — фаза, N — нулевой рабочий, PE — защитный проводник
- УЗИП (ограничитель перенапряжений), FV — марка
- ГЗШ — главная заземляющая шина; штрихпунктир — проводник основной системы уравнивания потенциалов (ОСУП)
- обрыв шины: схема продолжена на следующем листе
- резервный аппарат (не менее 20 % групп)

Данные щитка

Показатель	Значение
Номер щитка	ЩК
Тип	ЩРВ-П-54, IP41
Уст. мощность, кВт	30,4
Разреш. мощность, кВт	15
Расчётная, кВт	12,6
Автоматы 1п: занят. / рез.	17 / 4
Модулей: всего / занято	54 / 40
Ток на вводе, А	63
Вводной аппарат	QF0 C63, 2P
УЗИП	FV1, тип 2, ЩК, после счётчика
ГЗШ, проводник ОСУП	Cu 6 мм²
Листов схемы	2 (группы по листам)

Таблица групп щита ЩК и кабельный журнал

№	Назначение	Помещения	Автомат	УЗО / дифавтомат	Кабель	Длина, м	P, кВт	Точек
1	освещение 1-го этажа (гостиная-кухня, кабинет, холл, прихожая)	2, 3, 5, 6, 7, 8, 9, 10, 12	C10	30 мА, тип A	ВВГнг(A)-LS 3×1,5	70	0,8	53
2	освещение 2-го этажа (спальни, холл, гардеробная, кладовая)	1, 2, 5, 10, 11	C10	30 мА, тип A	ВВГнг(A)-LS 3×1,5	75	0,7	42
3	освещение и вентиляторы санузлов	4, 11, 13	C10	30 мА, тип A	ВВГнг(A)-LS 3×1,5	35	0,2	11
4	розетки гостиной (зона отдыха, ТВ, обеденная)	6	C16	30 мА, тип A	ВВГнг(A)-LS 3×2,5	35	2	6
5	розетки фартука кухни	3, 7, 12	C16	30 мА, тип A	ВВГнг(A)-LS 3×2,5	15	2,5	13
6	розетки кухни: холодильник, вытяжка, мелкая техника	1, 2, 5, 10	C16	30 мА, тип A	ВВГнг(A)-LS 3×2,5	18	1,5	11
7	варочная панель	1	C32	30 мА, тип A	ВВГнг(A)-LS 3×6	15	7	6
8	духовой шкаф	1	C16	30 мА, тип A	ВВГнг(A)-LS 3×2,5	15	3	1
9	посудомоечная машина	1	C16	30 мА, тип A	ВВГнг(A)-LS 3×2,5	15	2	1

Примечания

1. Схема однолинейная: одна линия — фаза, N и PE группы; аппараты — в отключённом положении (ГОСТ 2.702, ГОСТ 2.755). Номера групп — как у точек на планах (гр.). За отметку 0,000 принят уровень чистого пола; высота щита — по плану розеток.
2. Розеточные и мокрые линии — через УЗО или дифавтомат с током утечки не более 30 мА (ПУЭ 7.1.79); в санузле выполнить ДСУП (ПУЭ 7.1.87–7.1.88).
3. УЗО тип A — для линий с электроникой, стиральной и посудомоечной машиной, LED-драйверами; тип AC — только для чисто активной нагрузки.
4. Кабель — медный, исполнение нг(A)-LS (ГОСТ 31565-2012); скрытая прокладка только горизонтально и вертикально, фактические трассы зафиксировать исполнительной схемой до закрытия отделкой.
5. Номинал автомата — не выше допустимого тока кабеля: 1,5 мм² — до 10 А, 2,5 мм² — до 16 А. Резерв щита — не менее 20 % модулей.
6. Расчёт нагрузок, токов КЗ, селективности и сечений — по проекту ЭОМ организации с допуском СРО; лист задаёт состав, расположение и группы.
7. УЗИП FV1 — после вводного автомата, проводник к шине PE — кратчайший, без петель. Шина PE щита соединяется с ГЗШ проводником ОСУП; к ГЗШ присоединяются трубы водопровода и отопления на вводе в квартиру (ПУЭ 7.1.87). Шины N и PE — раздельные, после разделения PEN не объединяются.
8. До подключения нагрузки — приёмо-сдаточные испытания с протоколом: сопротивление изоляции линий не менее 0,5 МОм, срабатывание УЗО по току и времени, непрерывность защитных проводников PE (ПУЭ, гл. 1.8).

Допущения и предложения на листе

Основа листа: взаимное расположение помещений, контур дома 9600 × 8000 и раскладка этажей подобраны проектировщиком под габариты помещений брифа; обмер и проект АР — задание (К-1); высота потолка 2900 мм — по брифу, не замерена; перекрытие 330 мм и отметка 2-го этажа +3,230 приняты; проект КР — задание (К-2); наружные стены 400 мм, перегородки 120 мм приняты (в брифе толщин нет) (К-1); разрешённая мощность 15 кВт принята по типовым ТУ для частного дома (К-4).

Открытые вопросы и конфликты по листу: К-4.

См. лист открытых вопросов (лист 6, записи К-1, К-2, К-4).

Изм.	Кол.уч	Лист	№ док.	Подп.	Дата
Разраб.		Кырлан А.С.			19.10.26
Пров.					
ГИП					
Н. контр.					
Утв.					

ГД-2026-012-АИ

Дом 120 м²

Общая площадь 147,36* м² · * размеры приняты, не замерены (реестр — л. 6, К-1)

Дизайн-проект интерьера

Стадия	Лист	Листов
РП	36	130

Однолинейная схема щита

М б/м

Кырлан Александр Сергеевич

выпуск 19.10.2026 № 53e4f7ddae · стр. 40 из 160

Однолинейная схема щита (продолжение)

Щит квартирный ЩК · гр. 10—17 из 17 · без масштаба

ПРЕДВАРИТЕЛЬНО · не для производства работ · открыто пунктов: 6 (реестр — л. 6)

Продолжение однолинейной схемы щита ЩК, начало — лист 36

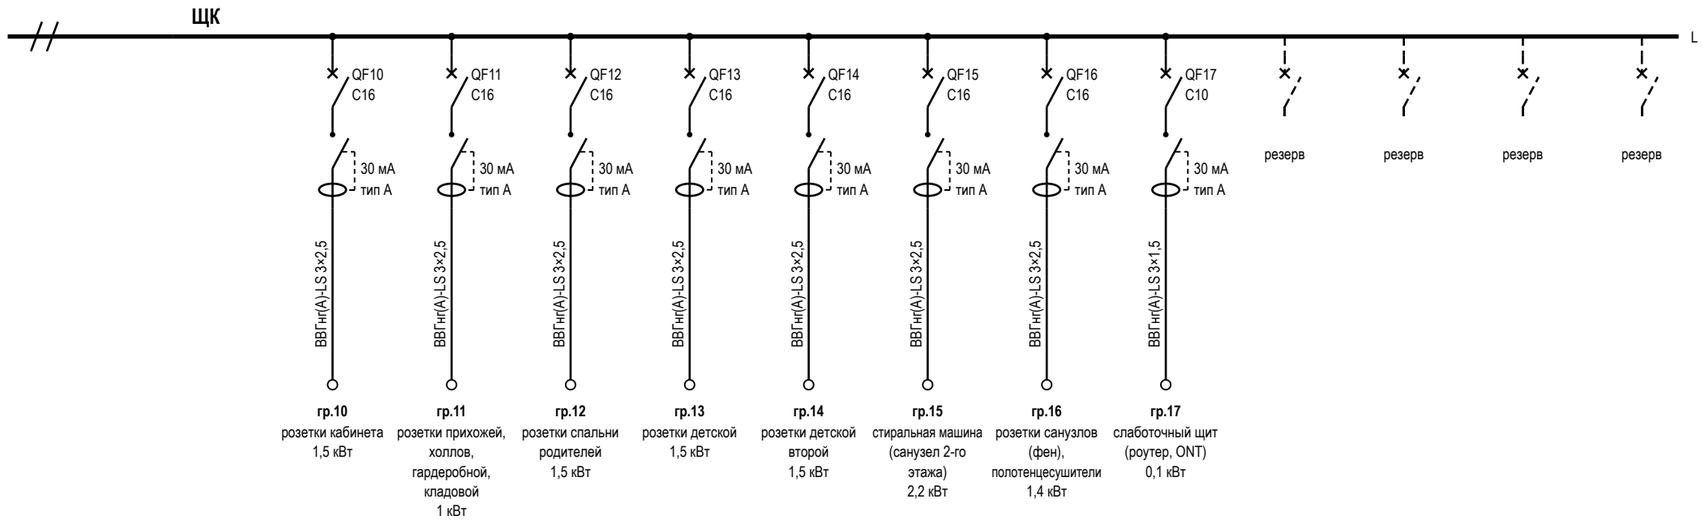

Таблица групп щита ЩК и кабельный журнал (продолжение)

№	Назначение	Помещения	Автомат	УЗО / дифавтомат	Кабель	Длина, м	Р, кВт	Точек
10	розетки кабинета	1	C16	30 мА, тип A	ВВГнг(A)-LS 3×2,5	20	1,5	1
11	розетки прихожей, холлов, гардеробной, кладовой	1, 11	C16	30 мА, тип A	ВВГнг(A)-LS 3×2,5	45	1	3
12	розетки спальни родителей	13	C16	30 мА, тип A	ВВГнг(A)-LS 3×2,5	30	1,5	1
13	розетки детской	4, 13	C16	30 мА, тип A	ВВГнг(A)-LS 3×2,5	30	1,5	3
14	розетки детской второй	5	C16	30 мА, тип A	ВВГнг(A)-LS 3×2,5	30	1,5	1
15	стиральная машина (санузел 2-го этажа)		C16	30 мА, тип A	ВВГнг(A)-LS 3×2,5	20	2,2	0
16	розетки санузлов (фен), полотенцесушители		C16	30 мА, тип A	ВВГнг(A)-LS 3×2,5	35	1,4	0
17	слаботочный щит (роутер, ONT)		C10	30 мА, тип A	ВВГнг(A)-LS 3×1,5	5	0,1	0
	Итого по сечениям ВВГнг(A)-LS (все группы щита), м: 3×1,5 — 185; 3×2,5 — 308; 3×6 — 15					508		

Примечания

1. Лист — продолжение однолинейной схемы щита ЩК: начало, данные щитка и условные обозначения — лист 36. Ввод, учёт, вводной аппарат, УЗИП, шины N и PE и ГЗШ показаны там же; шина L листа — та же шина щита.
2. Схема однолинейная: одна линия — фаза, N и PE группы; аппараты — в отключённом положении (ГОСТ 2.702, ГОСТ 2.755). Номера групп — как у точек на планах (гр.). За отметку 0,000 принят уровень чистого пола; высота щита — по плану розеток.
3. Розеточные и мокрые линии — через УЗО или дифавтомат с током утечки не более 30 мА (ПУЭ 7.1.79); в санузле выполнить ДСУП (ПУЭ 7.1.87–7.1.88).
4. УЗО тип A — для линий с электроникой, стиральной и посудомоечной машиной, LED-драйверами; тип AC — только для чисто активной нагрузки.
5. Кабель — медный, исполнение нг(A)-LS (ГОСТ 31565-2012); скрытая прокладка только горизонтально и вертикально, фактические трассы зафиксировать исполнительной схемой до закрытия отделкой.
6. Номинал автомата — не выше допустимого тока кабеля: 1,5 мм² — до 10 А, 2,5 мм² — до 16 А. Резерв щита — не менее 20 % модулей.
7. Расчёт нагрузок, токов КЗ, селективности и сечений — по проекту ЭОМ организации с допуском СРО; лист задаёт состав, расположение и группы.
8. До подключения нагрузки — приёмо-сдаточные испытания с протоколом: сопротивление изоляции линий не менее 0,5 МОм, срабатывание УЗО по току и времени, непрерывность защитных проводников PE (ПУЭ, гл. 1.8).

Допущения и предложения на листе

Основа листа: взаимное расположение помещений, контур дома 9600 × 8000 и раскладка этажей подобраны проектировщиком под габариты помещений брифа; обмер и проект АР — задание (К-1); высота потолка 2900 мм — по брифу, не замерена; перекрытие 330 мм и отметка 2-го этажа +3,230 приняты; проект КР — задание (К-2); наружные стены 400 мм, перегородки 120 мм приняты (в брифе толщин нет) (К-1); разрешённая мощность 15 кВт принята по типовым ТУ для частного дома (К-4).

См. лист открытых вопросов (лист 6, записи К-1, К-2, К-4).

Изм.	Кол.уч	Лист	№ док.	Подп.	Дата
Разраб.		Кырлан А.С.			19.10.26
Пров.					
ГИП					
Н. контр.					
Утв.					

ГД-2026-012-АИ

Дом 120 м²

Общая площадь 147,36* м² · * размеры приняты, не замерены (реестр — л. 6, К-1)

Дизайн-проект интерьера	Стадия	Лист	Листов
	РП	37	130
Однолинейная схема щита (продолжение) М б/м	**Кырлан Александр Сергеевич**		

выпуск 19.10.2026 № 53e4f7ddae · стр. 41 из 160

План принципиальных трасс · 1-й этаж

Силовые трассы и объёмы электромонтажа, слаботочка в объёмах · размеры в мм

ПРЕДВАРИТЕЛЬНО · не для производства работ · открыто пунктов: 6 (реестр — л. 6)

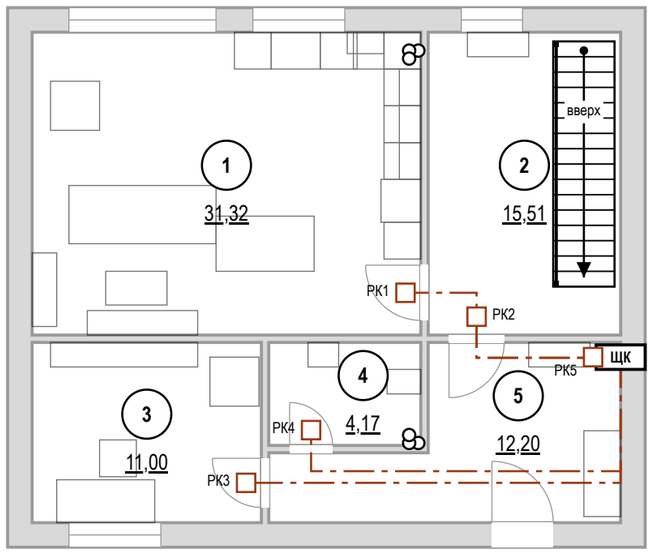

Кабель по группам ВВГнг(А)-LS, м

Гр.	мм²	Трасса	Данные
1	3×1,5	47,4	70
2	3×1,5	94,2	75
3	3×1,5	22,8	35
5	3×2,5	28,1	15
6	3×2,5	52,4	18
7	3×6	29,8	15

Гр.	мм²	Трасса	Данные
8	3×2,5	13,9	15
9	3×2,5	12,1	15
10	3×2,5	15,3	20
11	3×2,5	15,8	45
13	3×2,5	17,7	30
14	3×2,5	4,1	30
Σ		**353,6**	**508**

Экспликация помещений

№	Помещение	Площадь, м²
1	Гостиная-кухня	31,32
2	Холл с лестницей	15,51
3	Кабинет	11,00
4	Санузел гостевой	4,17
5	Прихожая	12,20
	Итого (общая площадь)	147,36

Объёмы прокладки

Работа, материал	Ед.	Кол.
Гофротруба Ø20 в потолочном пространстве	м	138,9
Кабель-канал плинтуса для силовых линий	м	87,7
Короб или накладной канал для вертикальных спусков и подъёмов	м	64,9
Коробка распределительная (РК) над дверью помещения	шт	5
Слаботочка: кабель домофона	м	6,1
Слаботочка: Кабель коаксиальный RG-6 (75 Ом) к розеткам ТВ	м	16,7
Слаботочка: U/UTP кат. 6 (LAN, Wi-Fi, камеры)	м	47,9
Слаботочка: гофротруба Ø20 отдельно от силовых	м	63,6

Штробы — только после заключения

Работа	Ед.	Кол.
Вертикальные штробы 20×20 мм от потолка до каждой настенной точки (в маршрут без штроб не входят)	м	89,96

Условные обозначения

- **ЩК** — щит квартирный
- РК — распределительная коробка над дверью помещения
- магистраль от щита к РК: потолочное пространство, гофра
- мебель и сантехприборы — подложка

Допущения и предложения на листе

Основа листа: взаимное расположение помещений, контур дома 9600 × 8000 и раскладка этажей подобраны проектировщиком под габариты помещений брифа; обмер и проект АР — задание (К-1); высота потолка 2900 мм — по брифу, не замерена; перекрытие 330 мм и отметка 2-го этажа +3,230 приняты; проект КР — задание (К-2); наружные стены 400 мм, перегородки 120 мм приняты (в брифе толщин нет) (К-1); разрешённая мощность 15 кВт принята по типовым ТУ для частного дома (К-4).

Знак «**» — предложение проектировщика, заказчиком не утверждено (согласовать с заказчиком): записи в реестре нет: ЩС — щит слаботочный: место и состав.

См. лист открытых вопросов (лист 6, записи К-1, К-2, К-4).

Примечания

1. За отметку 0,000 принят уровень чистого пола. Высоты Н — от чистого пола до оси изделия; привязки — от чистовой грани стены до оси механизма (у рамки на несколько постов — до оси рамки).
2. Розеточные и мокрые линии — через УЗО или дифавтомат с током утечки не более 30 мА (ПУЭ 7.1.79); в санузле выполнить ДСУП (ПУЭ 7.1.87–7.1.88).
3. Кабель — медный, исполнение нг(А)-LS (ГОСТ 31565-2012); скрытая прокладка только горизонтально и вертикально, фактические трассы зафиксировать исполнительной схемой до закрытия отделкой.
4. Расчёт нагрузок, токов КЗ, селективности и сечений — по проекту ЭОМ организации с допуском СРО; лист задаёт состав, расположение и группы.
5. Длины — по плану: от щита вверх в потолочное пространство, по дверям и коридору без захода в мокрые помещения к распределительной коробке над дверью, далее к точкам; вертикали считаются вниз и обратно (у последней точки цепочки — в один конец); запас 10 %. Трассы принципиальные: фактическую зафиксировать исполнительной схемой до закрытия отделкой.
6. Несущие стены не определены: штробы в стенах не выполнять. Маршрут проложен без штроб: горизонтали — за потолком в гофре (138,9 м) и в кабель-канале плинтуса (87,7 м), вертикали — в коробе или накладном канале (114,2 м кабеля). Точек: за потолком — 39, спуск из потолка — 6, по плинтусу — 14, плинтус и подъём — 23.
7. Вариант со штробами — работа после технического заключения: 89,96 м вертикальных штроб от потолка до каждой настенной точки; условие — только после технического заключения: стена не несущая (или вертикальная штроба в несущей согласована конструктором), глубина и ширина 20–25 мм, не в зонах 0–2 ванной. Без заключения и согласования конструктора в смету и в график эта работа не входит.
8. В данных проекта (журнал щита) длины кабеля внесены оценкой (508 м), по трассам из геометрии — 354 м (-30 %): к закупке и в смету принимать длины по трассам, а оценку в данных проекта заменить.
9. Слаботочные сети: кабели и точки считаются по лучам от ЩС** (лист слаботочных сетей): 71 м, портов патч-панели и коммутатора не менее 4; из точек 2 предложения листа слаботочки, не подтверждённые заказчиком. Изделия — в ведомости изделий.

1000 мм · печать 1:1

Изм.	Кол.уч	Лист	№ док.	Подп.	Дата
Разраб.		Кырлан А.С.			19.10.26
Пров.					
ГИП					
Н. контр.					
Утв.					

ГД-2026-012-АИ

Дом 120 м²

Общая площадь 147,36* м² · * размеры приняты, не замерены (реестр — л. 6, К-1)

Дизайн-проект интерьера

Стадия	Лист	Листов
РП	38	130

План принципиальных трасс · 1-й этаж

М 1:100

Кырлан Александр Сергеевич

выпуск 19.10.2026 № 53e4f7ddae · стр. 42 из 160

План принципиальных трасс · 2-й этаж

Силовые трассы и объёмы электромонтажа, слаботочка в объёмах · размеры в мм

ПРЕДВАРИТЕЛЬНО · не для производства работ · открыто пунктов: 6 (реестр — л. 6)

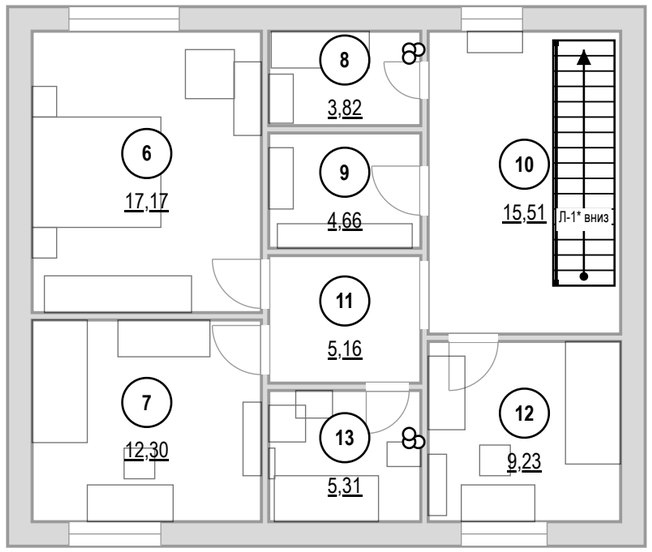

Трассы не построены

нет точки щита квартирного (points kind: panel) — трассу строить не от чего

Экспликация помещений

№	Помещение	Площадь, м²
6	Спальня родителей	17,17
7	Детская	12,30
8	Гардеробная	3,82
9	Кладовая	4,66
10	Холл второго этажа	15,51
11	Коридор второго этажа	5,16
12	Детская вторая	9,23
13	Санузел второго этажа	5,31
	Итого (общая площадь)	147,36

Условные обозначения

- ЩК — щит квартирный
- РК — распределительная коробка над дверью помещения
- магистраль от щита к РК: потолочное пространство, гофра
- мебель и сантехприборы — подложка

Допущения и предложения на листе

Основа листа: взаимное расположение помещений, контур дома 9600 × 8000 и раскладка этажей подобраны проектировщиком под габариты помещений брифа; обмер и проект АР — задание (К-1); высота потолка 2900 мм — по брифу, не замерена; перекрытие 330 мм и отметка 2-го этажа +3,230 приняты; проект КР — задание (К-2); наружные стены 400 мм, перегородки 120 мм приняты (в брифе толщин нет) (К-1); разрешённая мощность 15 кВт принята по типовым ТУ для частного дома (К-4).

Знак «*» — принято, не замерено и не подтверждено (замерить на объекте): К-3: Л-1 — место, тип и размеры лестницы брифом не заданы (только «лестница из холла 1-го этажа»): одномаршевая 17 × 190 × 250 вдоль стены Б холла — предложение проектировщика; конструкция и расчёт — проект КР.

См. лист открытых вопросов (лист 6, записи К-1–К-4).

Примечания

1. За отметку 0,000 принят уровень чистого пола. Высоты Н — от чистого пола до оси изделия; привязки — от чистовой грани стены до оси механизма (у рамки на несколько постов — до оси рамки).
2. Розеточные и мокрые линии — через УЗО или дифавтомат с током утечки не более 30 мА (ПУЭ 7.1.79); в санузле выполнить ДСУП (ПУЭ 7.1.87–7.1.88).
3. Кабель — медный, исполнение нг(А)-LS (ГОСТ 31565-2012); скрытая прокладка только горизонтально и вертикально, фактические трассы зафиксировать исполнительной схемой до закрытия отделкой.
4. Расчёт нагрузок, токов КЗ, селективности и сечений — по проекту ЭОМ организации с допуском СРО; лист задаёт состав, расположение и группы.
5. Щит квартиры (дома) — на 1-м этаже: кабели групп 2-й этаж поднимаются от щита в вертикальном кабель-канале (коробе) у лестницы и далее за потолком к точкам. Место короба и проход через перекрытие — задание конструктору; длины трасс этажа считаются после этого решения.

1000 мм · печать 1:1

Изм.	Кол.уч	Лист	№ док.	Подп.	Дата
Разраб.		Кырлан А.С.			19.10.26
Пров.					
ГИП					
Н. контр.					
Утв.					

ГД-2026-012-АИ

Дом 120 м²

Общая площадь 147,36* м² · * размеры приняты, не замерены (реестр — л. 6, К-1)

Дизайн-проект интерьера

Стадия	Лист	Листов
РП	39	130

План принципиальных трасс · 2-й этаж

М 1:100

Кырлан Александр Сергеевич

План слаботочных сетей · 1-й этаж

Интернет, ТВ, домофон · размеры в мм · высоты от чистого пола

ПРЕДВАРИТЕЛЬНО · не для производства работ · открыто пунктов: 6 (реестр — л. 6)

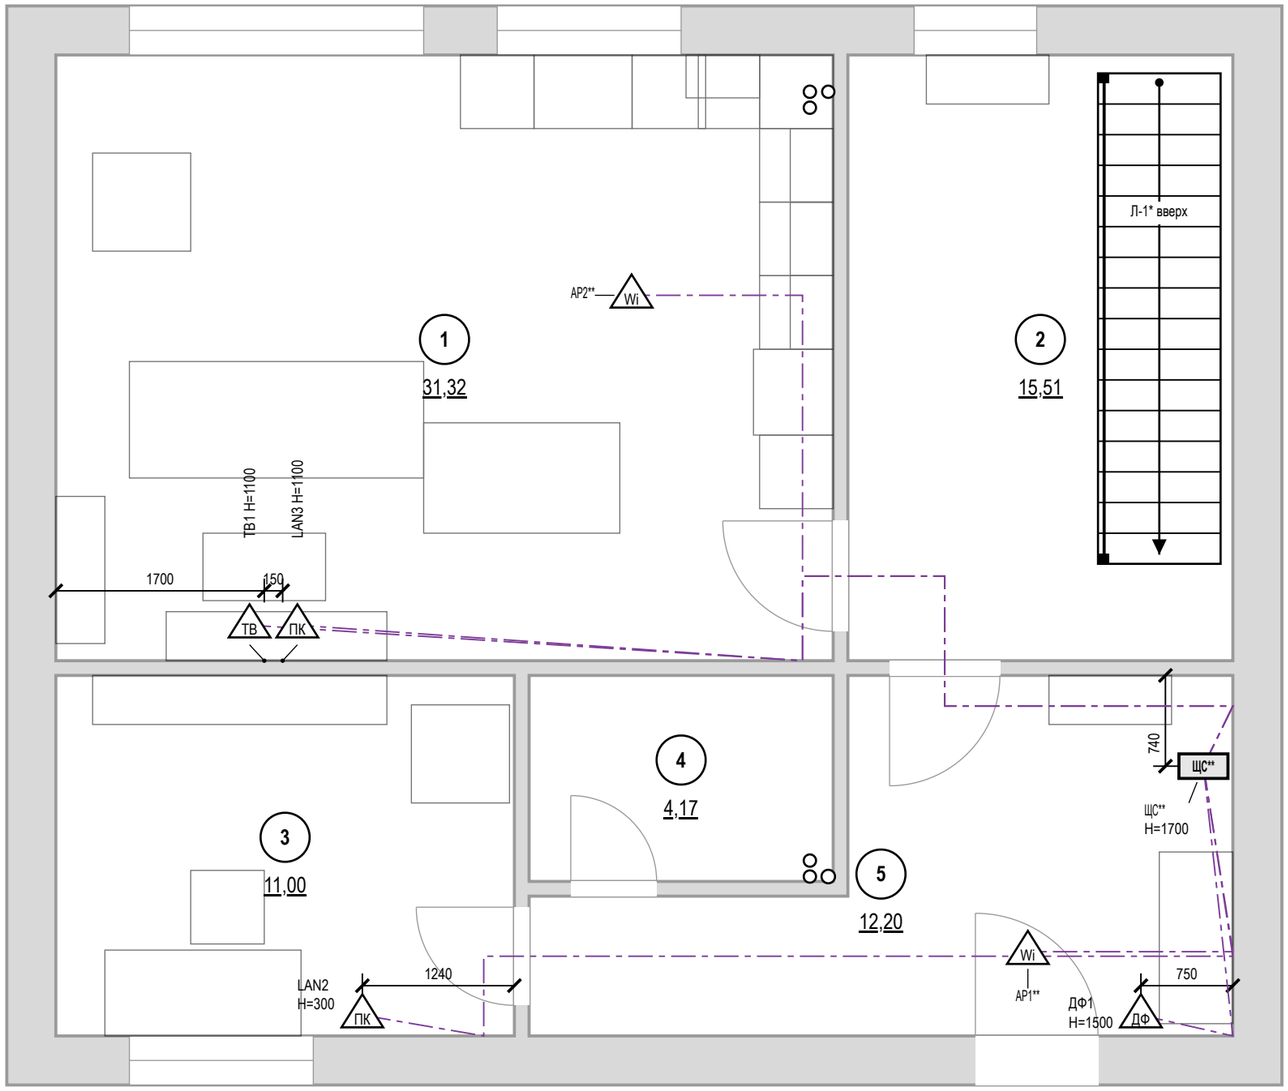

Ведомость слаботочных точек

Марка	Пом.	Назначение	H, мм	Кабель
TB1	1	розетка ТВ	1100	RG-6
LAN3	1	розетка LAN (RJ45)	1100	U/UTP кат. 6
AP2**	1	точка доступа Wi-Fi		U/UTP кат. 6
LAN2	3	розетка LAN (RJ45)	300	U/UTP кат. 6
ЩС**	5	щит слаботочный	1700	ввод пров.
ДФ1	5	домофон (трубка)	1500	по системе
AP1**	5	точка доступа Wi-Fi		U/UTP кат. 6

Условные обозначения

- **ЩС** — щит слаботочный: ввод провайдера, роутер, коммутатор
- ПК — розетка компьютерная RJ45
- ТВ — розетка телевизионная
- ДФ — трубка или монитор домофона
- Wi — точка доступа Wi-Fi (питание PoE)
- кабель от ЩС до точки, отдельным лучом
- мебель и сантехприборы — подложка
- (1) — номер помещения, площадь м²

Допущения и предложения на листе

Основа листа: взаимное расположение помещений, контур дома 9600 × 8000 и раскладка этажей подобраны проектировщиком под габариты помещений брифа; обмер и проект АР — задание (К-1); высота потолка 2900 мм — по брифу, не замерена; перекрытие 330 мм и отметка 2-го этажа +3,230 приняты; проект КР — задание (К-2); наружные стены 400 мм, перегородки 120 мм приняты (в брифе толщин нет) (К-1); разрешённая мощность 15 кВт принята по типовым ТУ для частного дома (К-4).

Знак «*» — принято, не замерено и не подтверждено (замерить на объекте): К-3: Л-1 — место, тип и размеры лестницы брифом не заданы (только «лестница из холла 1-го этажа»): одномаршевая 17 × 190 × 250 вдоль стены Б холла — предложение проектировщика; конструкция и расчёт — проект КР.

Знак «**» — предложение проектировщика, заказчиком не утверждено (согласовать с заказчиком): записи в реестре нет: AP2, AP1 — точка доступа Wi-Fi: число и места; ЩС — щит слаботочный: место и состав.

См. лист открытых вопросов (лист 6, записи К-1–К-4).

Примечания

1. За отметку 0,000 принят уровень чистого пола. Высоты H — от чистого пола до оси изделия; привязки — от чистовой грани стены до оси механизма (у рамки на несколько постов — до оси рамки).
2. Высота установки, не указанная на плане: розетки LAN и ТВ — 300 мм от чистого пола.
3. Слаботочные кабели — отдельно от силовых: в своей трубе или лотке, при параллельной прокладке не ближе 100 мм к силовым, пересечения под прямым углом; каждую точку — отдельным кабелем от ЩС** без скруток.
4. Трассы на листе — принципиальные; фактические зафиксировать исполнительной схемой до закрытия отделкой. Силовые линии, УЗО 30 мА, ДСУП, кабель нг(A)-LS — по листам розеток и щита.
5. Проект силовой части и расчёт токов КЗ — по проекту ЭОМ; слаботочная часть согласуется с провайдером и управляющей компанией (домофон, коллективное ТВ).

1000 мм · печать 1:1

Изм.	Кол.уч	Лист	№ док.	Подп.	Дата
Разраб.		Кырлан А.С.			19.10.26
Пров.					
ГИП					
Н. контр.					
Утв.					

ГД-2026-012-АИ

Дом 120 м²

Общая площадь 147,36* м² · * размеры приняты, не замерены (реестр — л. 6, К-1)

Дизайн-проект интерьера	Стадия	Лист	Листов
	РП	40	130

План слаботочных сетей · 1-й этаж

М 1:50

Кырлан Александр Сергеевич

выпуск 19.10.2026 № 53e4f7ddae · стр. 44 из 160

План слаботочных сетей · 2-й этаж

Интернет, ТВ, домофон · размеры в мм · высоты от чистого пола

ПРЕДВАРИТЕЛЬНО · не для производства работ · открыто пунктов: 6 (реестр — л. 6)

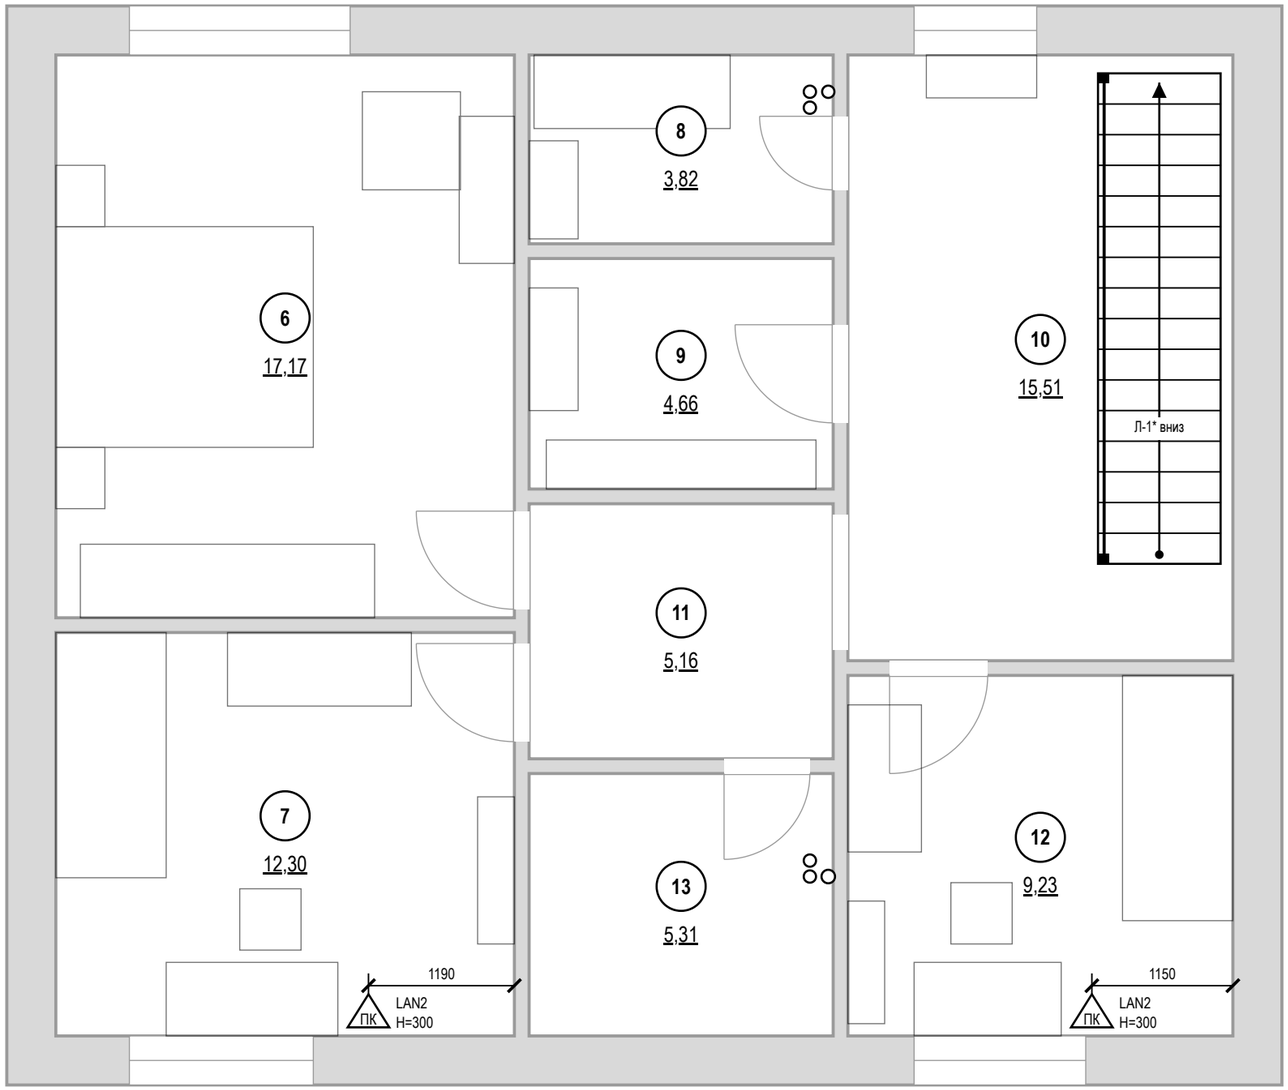

Ведомость слаботочных точек

Марка	Пом.	Назначение	H, мм	Кабель
LAN2	7	розетка LAN (RJ45)	300	U/UTP кат. 6
LAN2	12	розетка LAN (RJ45)	300	U/UTP кат. 6

Условные обозначения

ПК — розетка компьютерная RJ45

мебель и сантехприборы — подложка

1 — номер помещения, площадь м²

Допущения и предложения на листе

Основа листа: взаимное расположение помещений, контур дома 9600 × 8000 и раскладка этажей подобраны проектировщиком под габариты помещений брифа; обмер и проект АР — задание (К-1); высота потолка 2900 мм — по брифу, не замерена; перекрытие 330 мм и отметка 2-го этажа +3,230 приняты; проект КР — задание (К-2); наружные стены 400 мм, перегородки 120 мм приняты (в брифе толщин нет) (К-1); разрешённая мощность 15 кВт принята по типовым ТУ для частного дома (К-4).

Знак «*» — принято, не замерено и не подтверждено (замерить на объекте): К-3: Л-1 — место, тип и размеры лестницы брифом не заданы (только «лестница из холла 1-го этажа»): одномаршевая 17 × 190 × 250 вдоль стены Б холла — предложение проектировщика; конструкция и расчёт — проект КР.

Знак «**» — предложение проектировщика, заказчиком не утверждено (согласовать с заказчиком): записи в реестре нет: ЩС — щит слаботочный: место и состав.

См. лист открытых вопросов (лист 6, записи К-1–К-4).

Примечания

1. За отметку 0,000 принят уровень чистого пола. Высоты H — от чистого пола до оси изделия; привязки — от чистовой грани стены до оси механизма (у рамки на несколько постов — до оси рамки).
2. Высота установки, не указанная на плане: розетки LAN и ТВ — 300 мм от чистого пола.
3. Слаботочные кабели — отдельно от силовых: в своей трубе или лотке, при параллельной прокладке не ближе 100 мм к силовым, пересечения под прямым углом; каждую точку — отдельным кабелем от ЩС** без скруток.
4. Трассы на листе — принципиальные; фактические зафиксировать исполнительной схемой до закрытия отделкой. Силовые линии, УЗО 30 мА, ДСУП, кабель нг(A)-LS — по листам розеток и щита.
5. Проект силовой части и расчёт токов КЗ — по проекту ЭОМ; слаботочная часть согласуется с провайдером и управляющей компанией (домофон, коллективное ТВ).

1000 мм · печать 1:1

Изм.	Кол.уч	Лист	№ док.	Подп.	Дата
Разраб.		Кырлан А.С.			19.10.26
Пров.					
ГИП					
Н. контр.					
Утв.					

ГД-2026-012-АИ

Дом 120 м²

Общая площадь 147,36* м² · * размеры приняты, не замерены (реестр — л. 6, К-1)

Дизайн-проект интерьера

Стадия	Лист	Листов
РП	41	130

План слаботочных сетей · 2-й этаж

М 1:50

Кырлан Александр Сергеевич

выпуск 19.10.2026 № 53e4f7ddae · стр. 45 из 160

План вентиляции · 1-й этаж

Вытяжка, приток, переток · кондиционирование не предусмотрено · размеры в мм · высоты от чистого пола

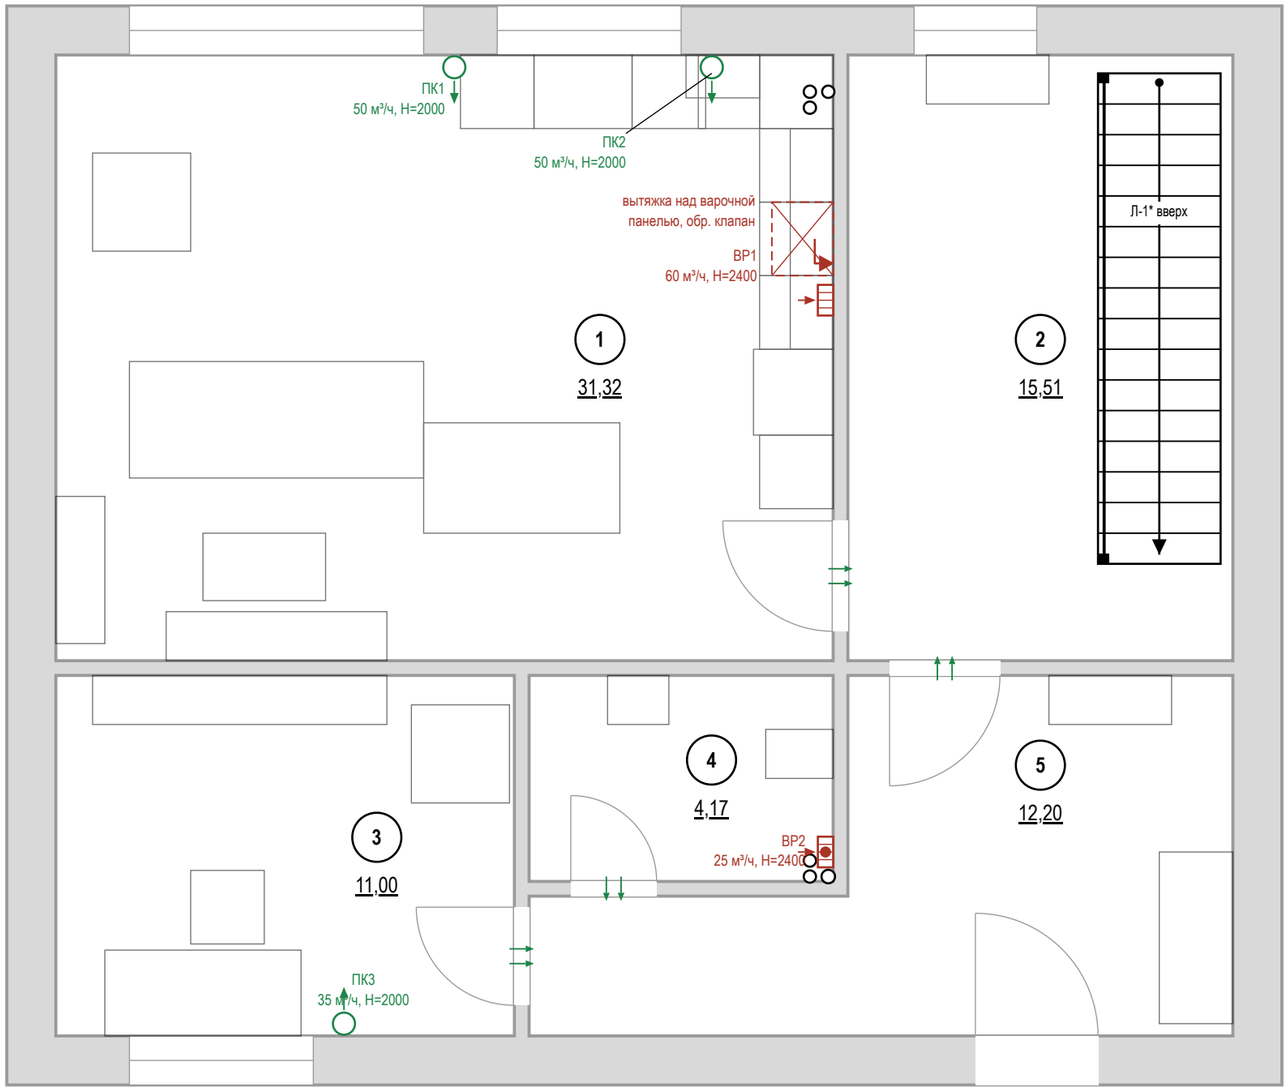

Условные обозначения

- стояк: К1 — канализация, В1 — ХВС, Т3 — ГВС
- номер помещения, площадь м²
- вытяжная решётка в вентканал: марка, расход м³/ч, H центра от чистого пола
- вытяжная решётка с бытовым вентилятором и обратным клапаном: марка, расход, H
- приточный клапан (КИВ) в наружной стене: марка, расход, H центра
- переток: зазор под полотном или переточная решётка
- кухонная вытяжка над варочной панелью
- воздуховод кухонной вытяжки в коробе под потолком
- отдельный вход воздуховода в вентканал, обратный клапан

Воздухообмен, м³/ч

№	Помещение	Выт. норма	Выт. проект	Прит. норма	Прит. проект	Устрой ства
1	Гостиная-кухня	60	60	94	100	ВР1, ПК1, ПК2
3	Кабинет			33	35	ПК3
4	Санузел гостевой	25	25			ВР2
	Итого	**85**	**85**	**120**	**135**	

Воздухообмен квартиры — по большей из сумм притока и вытяжки: норма 120 м³/ч, проект 135 м³/ч.
Приток больше вытяжки на 50 м³/ч — поднять вытяжку.

Допущения и предложения на листе

Основа листа: взаимное расположение помещений, контур дома 9600 × 8000 и раскладка этажей подобраны проектировщиком под габариты помещений брифа; обмер и проект АР — задание (К-1); высота потолка 2900 мм — по брифу, не замерена; перекрытие 330 мм и отметка 2-го этажа +3,230 приняты; проект КР — задание (К-2); наружные стены 400 мм, перегородки 120 мм приняты (в брифе толщин нет) (К-1); разрешённая мощность 15 кВт принята по типовым ТУ для частного дома (К-4).
Знак «*» — принято, не замерено и не подтверждено (замерить на объекте): К-3: Л-1 — место, тип и размеры лестницы брифом не заданы (только «лестница из холла 1-го этажа»): одномаршевая 17 × 190 × 250 вдоль стены Б холла — предложение проектировщика; конструкция и расчёт — проект КР.
См. лист открытых вопросов (лист 6, записи К-1–К-4).

Примечания

1. Расчёт систем ОВ и подбор оборудования — проектная организация с допуском СРО; лист даёт места, трассы и привязки.
2. Нормы вытяжки — СП 54.13330.2022 (Изм. 1, 2), табл. 7.1: кухня с электроплитой 60 м³/ч, с газовой 100; ванная и совмещённый санузел 50; уборная 25; гардеробная 0,2 ч⁻¹. Приток в жилые — 3 м³/ч на 1 м² (менее 20 м² общей площади на человека), иначе 30 м³/ч на человека.
3. Венткаталы и шахты не сужать, не переносить и не закрывать; вентилятор и кухонная вытяжка — через обратный клапан, без перекрытия естественной тяги.
4. Проектные расходы — не ниже нормы, вытяжка сведена с притоком вентиляторами мокрых помещений. Клапаны — в простенке у окна, центр 2000 мм, не над кроватью, не ближе 300 мм к стоякам отопления; типоразмер — на расход.
5. Кухонная вытяжка в воздухообмен не включена: воздуховод не менее Ø125 в коробе, вход в канал отдельный.
6. Переток — зазор под полотнами межкомнатных дверей или переточная решётка.
7. Кондиционирование заданием не предусмотрено; при установке трассы фреона и дренажа (не менее 40 мм/м, в К1 через сифон) и питание заложить до черновых работ.
8. Привязки оборудования — по паспортам приобретённых моделей, до черновых работ.

1000 мм · печать 1:1

Изм.	Кол.уч	Лист	№ док.	Подп.	Дата
Разраб.		Кырлан А.С.			19.10.26
Пров.					
ГИП					
Н. контр.					
Утв.					

ГД-2026-012-АИ

Дом 120 м²

Общая площадь 147,36* м² · * размеры приняты, не замерены (реестр — л. 6, К-1)

Дизайн-проект интерьера

Стадия	Лист	Листов
РП	42	130

План вентиляции · 1-й этаж

М 1:50

Кырлан Александр Сергеевич

ПРЕДВАРИТЕЛЬНО · не для производства работ · открыто пунктов: 6 (реестр — л. 6)

выпуск 19.10.2026 № 53e4f7ddae · стр. 46 из 160

План вентиляции · 2-й этаж

Вытяжка, приток, переток · кондиционирование не предусмотрено · размеры в мм · высоты от чистого пола

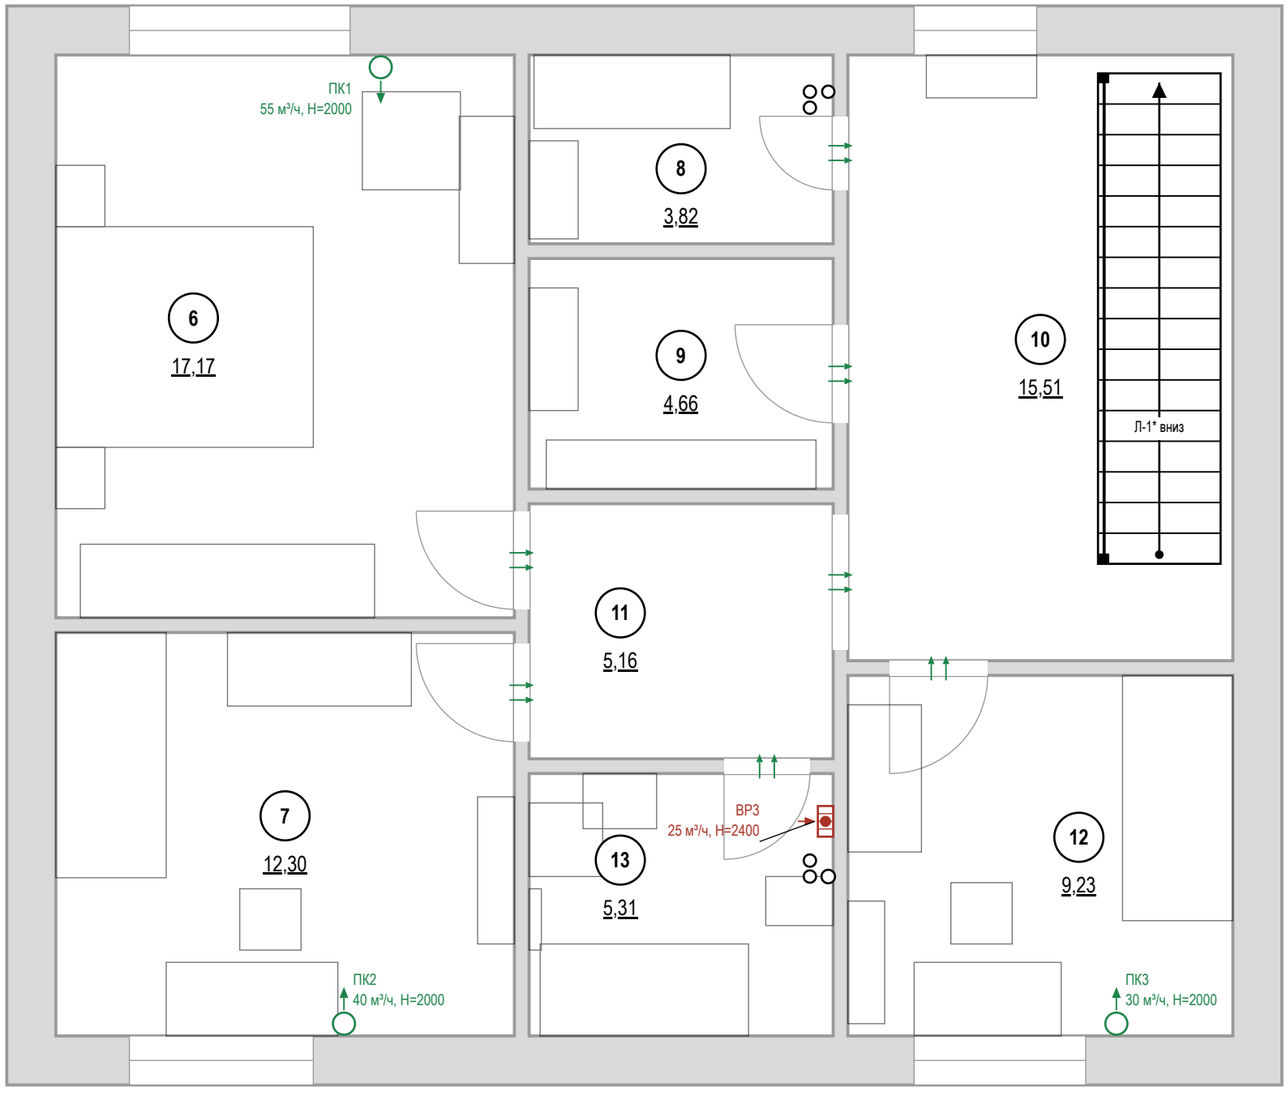

Условные обозначения

- стояк: К1 — канализация, В1 — ХВС, Т3 — ГВС
- 1 — номер помещения, площадь м²
- вытяжная решётка с бытовым вентилятором и обратным клапаном: марка, расход, Н
- приточный клапан (КИВ) в наружной стене: марка, расход, Н центра
- переток: зазор под полотном или переточная решётка

Воздухообмен, м³/ч

№	Помещение	Выт. норма	Выт. проект	Прит. норма	Прит. проект	Устрой ства
6	Спальня родителей			52	55	ПК1
7	Детская			37	40	ПК2
8	Гардеробная	2				переток
9	Кладовая	3				переток
12	Детская вторая			28	30	ПК3
13	Санузел второго этажа	50	**25 !**			ВР3
	Итого	**55**	**25**	**120**	**125**	

Воздухообмен квартиры — по большей из сумм притока и вытяжки: норма 120 м³/ч, проект 125 м³/ч.
Приток больше вытяжки на 100 м³/ч — поднять вытяжку.
«!» — проект ниже нормы.

Допущения и предложения на листе

Основа листа: взаимное расположение помещений, контур дома 9600 × 8000 и раскладка этажей подобраны проектировщиком под габариты помещений брифа; обмер и проект АР — задание (К-1); высота потолка 2900 мм — по брифу, не замерена; перекрытие 330 мм и отметка 2-го этажа +3,230 приняты; проект КР — задание (К-2); наружные стены 400 мм, перегородки 120 мм приняты (в брифе толщин нет) (К-1); разрешённая мощность 15 кВт принята по типовым ТУ для частного дома (К-4).
Знак «*» — принято, не замерено и не подтверждено (замерить на объекте): К-3: Л-1 — место, тип и размеры лестницы брифом не заданы (только «лестница из холла 1-го этажа»): одномаршевая 17 × 190 × 250 вдоль стены Б холла — предложение проектировщика; конструкция и расчёт — проект КР.
См. лист открытых вопросов (лист 6, записи К-1–К-4).

Примечания

1. Расчёт систем ОВ и подбор оборудования — проектная организация с допуском СРО; лист даёт места, трассы и привязки.
2. Нормы вытяжки — СП 54.13330.2022 (Изм. 1, 2), табл. 7.1: кухня с электроплитой 60 м³/ч, с газовой 100; ванная и совмещённый санузел 50; уборная 25; гардеробная 0,2 ч⁻¹. Приток в жилые — 3 м³/ч на 1 м² (менее 20 м² общей площади на человека), иначе 30 м³/ч на человека.
3. Вентканалы и шахты не сужать, не переносить и не закрывать; вентилятор и кухонная вытяжка — через обратный клапан, без перекрытия естественной тяги.
4. Проектные расходы — не ниже нормы, вытяжка сведена с притоком вентиляторами мокрых помещений. Клапаны — в простенке у окна, центр 2000 мм, не над кроватью, не ближе 300 мм к стоякам отопления; типоразмер — на расход.
5. Переток — зазор под полотнами межкомнатных дверей или переточная решётка.
6. Кондиционирование заданием не предусмотрено; при установке трассы фреона и дренажа (не менее 40 мм/м, в К1 через сифон) и питание заложить до черновых работ.
7. Привязки оборудования — по паспортам приобретённых моделей, до черновых работ.

1000 мм · печать 1:1

Изм.	Кол.уч	Лист	№ док.	Подп.	Дата
Разраб.		Кырлан А.С.			19.10.26
Пров.					
ГИП					
Н. контр.					
Утв.					

ГД-2026-012-АИ

Дом 120 м²

Общая площадь 147,36* м² · * размеры приняты, не замерены (реестр — л. 6, К-1)

Дизайн-проект интерьера

Стадия	Лист	Листов
РП	43	130

План вентиляции · 2-й этаж

М 1:50

Кырлан Александр Сергеевич

выпуск 19.10.2026 № 53e4f7ddae · стр. 47 из 160

План отопления · 1-й этаж

Радиаторы, стояки, подводки · размеры в мм · высоты от чистого пола

ПРЕДВАРИТЕЛЬНО · не для производства работ · открыто пунктов: 6 (реестр — л. 6)

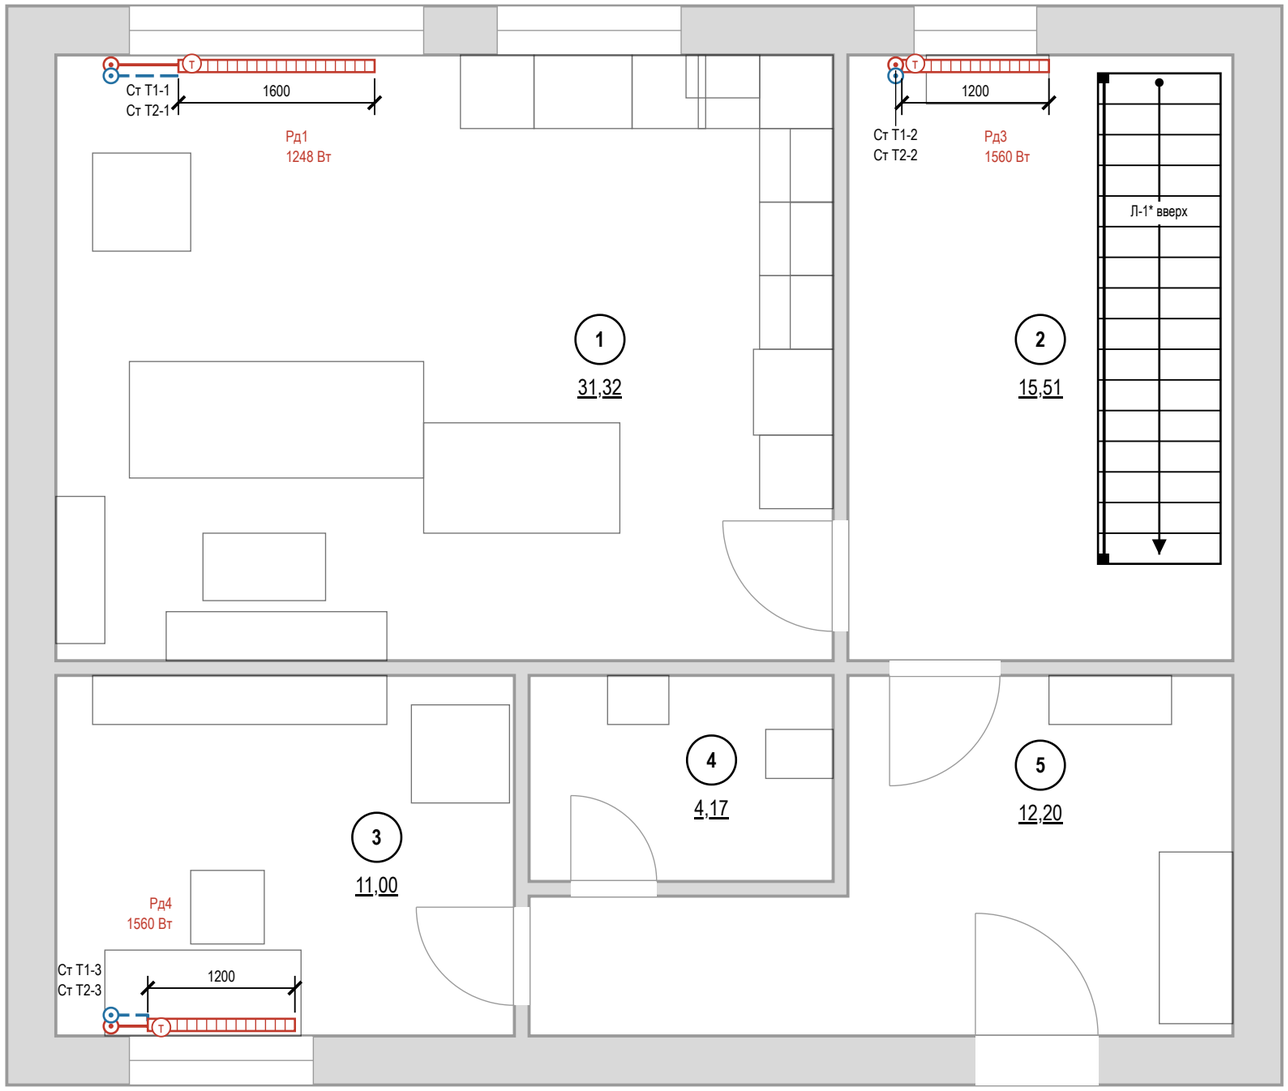

Условные обозначения

- (1) — номер помещения, площадь м²
- радиатор отопления (марка РО-N, длина по плану)
- (Т) — клапан с термоголовкой на подаче
- стояк отопления, подающий (Ст Т1-N)
- стояк отопления, обратный (Ст Т2-N)
- Т1 — отопление, подающий трубопровод
- Т2 — отопление, обратный трубопровод

Ведомость радиаторов

Марка	Помещение	Тип	Д×В×Г, мм	Низ / стена	Q, Вт
Рд1	1. Гостиная-кухня	панельный 22	1600×300×100	100 / 40	1248
Рд3	2. Холл с лестницей	панельный 22	1200×500×100	100 / 40	1560
Рд4	3. Кабинет	панельный 22	1200×500×100	100 / 40	1560

Низ — от чистого пола, стена — зазор до задней панели, мм.

Привязки — до обмера

Стояки отопления в исходных данных не заданы: показаны у откосов окон, подводки — принципиально. До черновых работ — обмер стояков и паспорта приборов; лист перевыпустить по факту.

Примечания

1. Расчёт системы отопления, теплопотерь и подбор приборов — проектная организация с допуском СРО; лист даёт места и привязки.
2. Тип, длина и мощность радиаторов — по теплотехническому расчёту; лист задаёт места, зазоры и подключение.
3. Зазоры радиатора: низ не менее 100 мм от чистого пола, верх не менее 100 мм до подоконника, 30–50 мм от стены до задней панели; центр по оси окна с допуском ±20 мм.
4. Радиаторы не закрывать глухими коробами и мебелью; перенос и замена приборов в многоквартирном доме — переустройство, согласование с управляющей организацией (ЖК РФ ст. 25–26); вынос на лоджию запрещён.
5. Трубы отопления через межквартирные стены не прокладывать (СП 51.13330.2011, п. 9.19); через перекрытия и перегородки — в гильзах.
6. Привязки приборов и подводок — по паспортам приобретённых радиаторов и клапанов, до черновых работ.
7. До закрытия отделкой трубопроводы отопления испытать гидростатическим давлением с оформлением акта (СП 73.13330.2016, 7.2–7.3).

Допущения и предложения на листе

Основа листа: взаимное расположение помещений, контур дома 9600 × 8000 и раскладка этажей подобраны проектировщиком под габариты помещений брифа; обмер и проект АР — задание (К-1); высота потолка 2900 мм — по брифу, не замерена; перекрытие 330 мм и отметка 2-го этажа +3,230 приняты; проект КР — задание (К-2); наружные стены 400 мм, перегородки 120 мм приняты (в брифе толщин нет) (К-1); разрешённая мощность 15 кВт принята по типовым ТУ для частного дома (К-4).
Знак «*» — принято, не замерено и не подтверждено (замерить на объекте): К-3: Л-1 — место, тип и размеры лестницы брифом не заданы (только «лестница из холла 1-го этажа»): одномаршевая 17 × 190 × 250 вдоль стены Б холла — предложение проектировщика; конструкция и расчёт — проект КР.
Открытые вопросы и конфликты по листу: К-6.
См. лист открытых вопросов (лист 6, записи К-1–К-4, К-6).

1000 мм · печать 1:1

Изм.	Кол.уч	Лист	№ док.	Подп.	Дата
Разраб.		Кырлан А.С.			19.10.26
Пров.					
ГИП					
Н. контр.					
Утв.					

ГД-2026-012-АИ

Дом 120 м²

Общая площадь 147,36* м² · * размеры приняты, не замерены (реестр — л. 6, К-1)

Дизайн-проект интерьера

Стадия	Лист	Листов
РП	44	130

План отопления · 1-й этаж

М 1:50

Кырлан Александр Сергеевич

выпуск 19.10.2026 № 53e4f7ddae · стр. 48 из 160

План отопления · 2-й этаж

Радиаторы, стояки, подводки · размеры в мм · высоты от чистого пола

ПРЕДВАРИТЕЛЬНО · не для производства работ · открыто пунктов: 6 (реестр — л. 6)

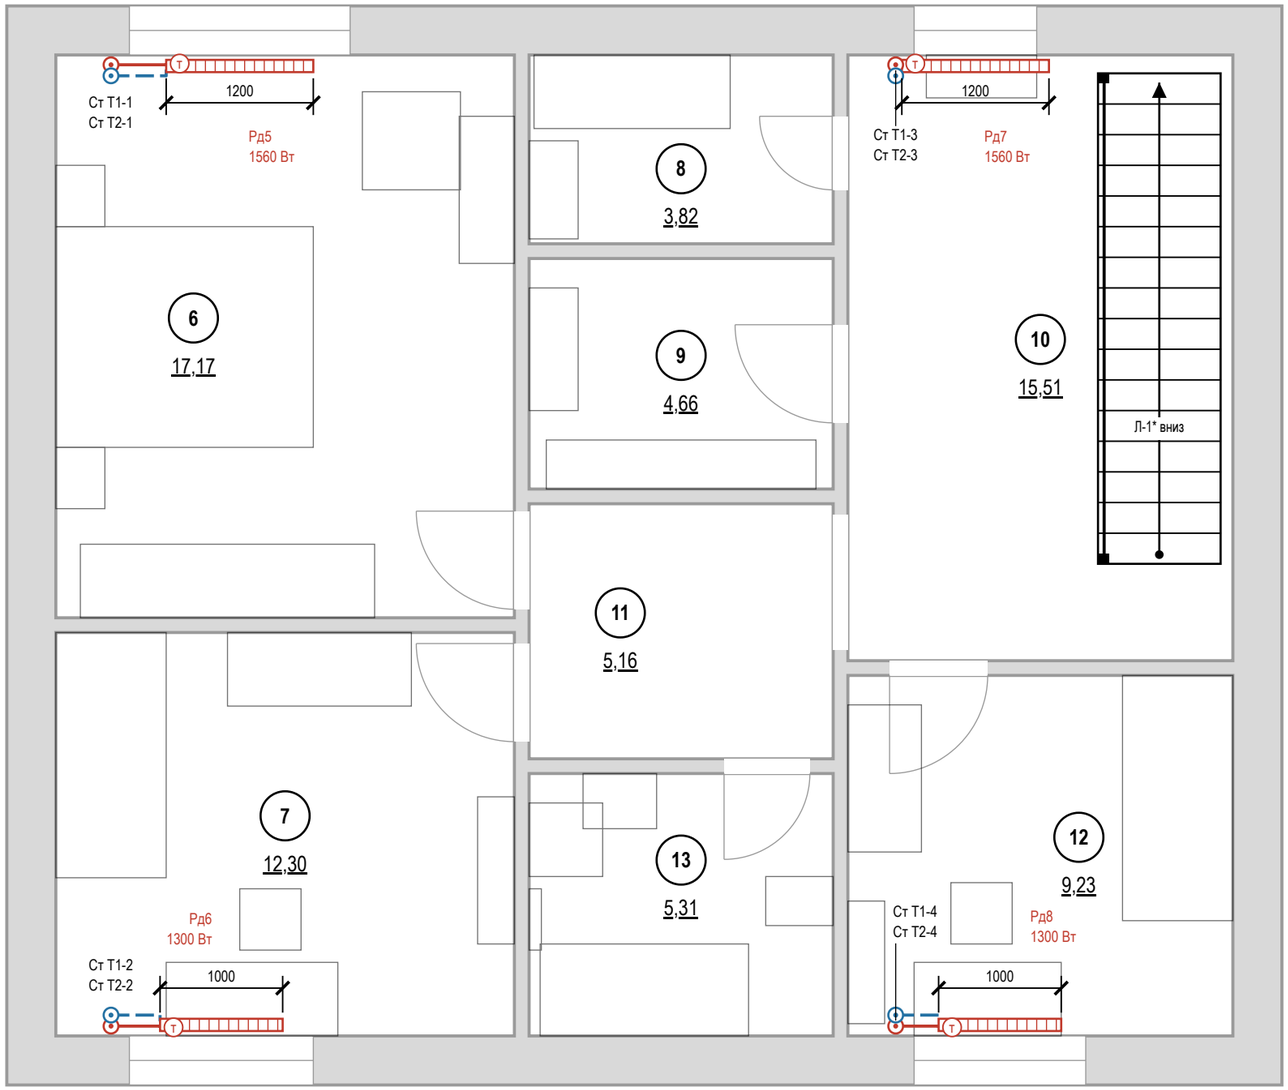

Условные обозначения

- (1) — номер помещения, площадь м²
- радиатор отопления (марка РО-N, длина по плану)
- (Т) — клапан с термоголовкой на подаче
- стояк отопления, подающий (Ст Т1-N)
- стояк отопления, обратный (Ст Т2-N)
- Т1 — отопление, подающий трубопровод
- Т2 — отопление, обратный трубопровод

Ведомость радиаторов

Марка	Помещение	Тип	Д×В×Г, мм	Низ / стена	Q, Вт
Рд5	6. Спальня родителей	панельный 22	1200×500×100	100 / 40	1560
Рд6	7. Детская	панельный 22	1000×500×100	100 / 40	1300
Рд7	10. Холл второго этажа	панельный 22	1200×500×100	100 / 40	1560
Рд8	12. Детская вторая	панельный 22	1000×500×100	100 / 40	1300

Низ — от чистого пола, стена — зазор до задней панели, мм.

Привязки — до обмера

Стояки отопления в исходных данных не заданы: показаны у откосов окон, подводки — принципиально. До черновых работ — обмер стояков и паспорта приборов; лист перевыпустить по факту.

Примечания

1. Расчёт системы отопления, теплопотерь и подбор приборов — проектная организация с допуском СРО; лист даёт места и привязки.
2. Тип, длина и мощность радиаторов — по теплотехническому расчёту; лист задаёт места, зазоры и подключение.
3. Зазоры радиатора: низ не менее 100 мм от чистого пола, верх не менее 100 мм до подоконника, 30–50 мм от стены до задней панели; центр по оси окна с допуском ±20 мм.
4. Радиаторы не закрывать глухими коробами и мебелью; перенос и замена приборов в многоквартирном доме — переустройство, согласование с управляющей организацией (ЖК РФ ст. 25–26); вынос на лоджию запрещён.
5. Трубы отопления через межквартирные стены не прокладывать (СП 51.13330.2011, п. 9.19); через перекрытия и перегородки — в гильзах.
6. Привязки приборов и подводок — по паспортам приобретённых радиаторов и клапанов, до черновых работ.
7. До закрытия отделкой трубопроводы отопления испытать гидростатическим давлением с оформлением акта (СП 73.13330.2016, 7.2–7.3).

Допущения и предложения на листе

Основа листа: взаимное расположение помещений, контур дома 9600 × 8000 и раскладка этажей подобраны проектировщиком под габариты помещений брифа; обмер и проект АР — задание (К-1); высота потолка 2900 мм — по брифу, не замерена; перекрытие 330 мм и отметка 2-го этажа +3,230 приняты; проект КР — задание (К-2); наружные стены 400 мм, перегородки 120 мм приняты (в брифе толщин нет) (К-1); разрешённая мощность 15 кВт принята по типовым ТУ для частного дома (К-4).
Знак «*» — принято, не замерено и не подтверждено (замерить на объекте): К-3: Л-1 — место, тип и размеры лестницы брифом не заданы (только «лестница из холла 1-го этажа»): одномаршевая 17 × 190 × 250 вдоль стены Б холла — предложение проектировщика; конструкция и расчёт — проект КР.
Открытые вопросы и конфликты по листу: К-6.
См. лист открытых вопросов (лист 6, записи К-1–К-4, К-6).

1000 мм · печать 1:1

Изм.	Кол.уч	Лист	№ док.	Подп.	Дата
Разраб.		Кырлан А.С.			19.10.26
Пров.					
ГИП					
Н. контр.					
Утв.					

ГД-2026-012-АИ

Дом 120 м²

Общая площадь 147,36* м² · * размеры приняты, не замерены (реестр — л. 6, К-1)

Дизайн-проект интерьера

Стадия	Лист	Листов
РП	45	130

План отопления · 2-й этаж

М 1:50

Кырлан Александр Сергеевич

выпуск 19.10.2026 № 53e4f7ddae · стр. 49 из 160

План выводов сантехники · 1-й этаж

Выводы В1, Т3, К1 · привязки от чистовых стен · высоты от чистого пола, мм

ПРЕДВАРИТЕЛЬНО · не для производства работ · открыто пунктов: 6 (реестр — л. 6)

Допущения и предложения на листе

Основа листа: взаимное расположение помещений, контур дома 9600 × 8000 и раскладка этажей подобраны проектировщиком под габариты помещений брифа; обмер и проект АР — задание (К-1); высота потолка 2900 мм — по брифу, не замерена; перекрытие 330 мм и отметка 2-го этажа +3,230 приняты; проект КР — задание (К-2); наружные стены 400 мм, перегородки 120 мм приняты (в брифе толщин нет) (К-1); разрешённая мощность 15 кВт принята по типовым ТУ для частного дома (К-4).

См. лист открытых вопросов (лист 6, записи К-1, К-2, К-4).

Фрагмент 1. Санузел гостевой (пом. 4)

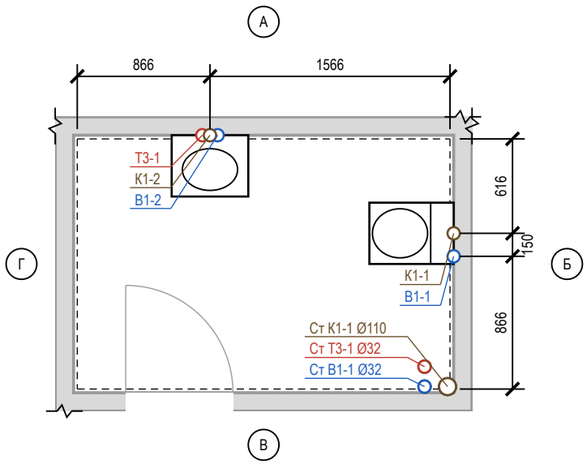

Фрагмент 2. Гостиная-кухня (пом. 1)

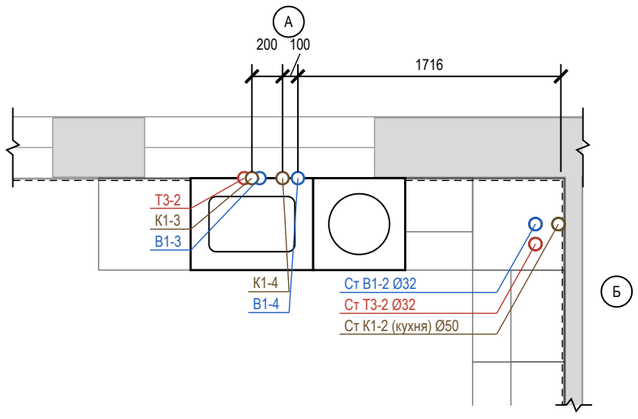

Ведомость привязок выводов

Код	Прибор	Ø	H, мм	Привязка от чист. стен, мм	Прим.
В1-1	Ст1 унитаз подвесной	½"	250*	ст. Б: 766 от А	в раме инсталляции
К1-1	Ст1 унитаз подвесной	Ø110	220*	ст. Б: 616 от А	
В1-2	Ст2 умывальник	½"	600*	ст. А: 916 от Г	межос. 100
Т3-1	Ст2 умывальник	½"	600*	ст. А: 816 от Г	межос. 100
К1-2	Ст2 умывальник	Ø50	500*	ст. А: 866 от Г	
В1-3	П3 мойка кухонная	½"	600*	ст. А: 1966 от Б	межос. 100
Т3-2	П3 мойка кухонная	½"	600*	ст. А: 2066 от Б	межос. 100
К1-3	П3 мойка кухонная	Ø50	400*	ст. А: 2016 от Б	
В1-4	П4 посудомоечная машина	½"	550*	ст. А: 1716 от Б	кран ПММ в шкафу мойки
К1-4	П4 посудомоечная машина	Ø40	550*	ст. А: 1816 от Б	слив ПММ в шкафу мойки

* — высота по практике монтажа; сверить по паспорту прибора

Условные обозначения

- вывод В1 (код — в ведомости привязок)
- вывод Т3 (код — в ведомости привязок)
- вывод К1 (код — в ведомости привязок)
- сантехприбор по расстановке (габарит модели)
- чистовая поверхность стены (от неё привязки)
- стояк «Ст К1-N / Ст В1-N» (ГОСТ 21.601), Ø мм
- линия обрыва (граница фрагмента)
- А — обозначение стены А–Г (как на развёртках)

Примечания

1. Привязки выводов даны от чистовых поверхностей стен (облицовка на сторону: санузел гостевой — 24 мм (штукатурка 10 + клей 5 + плитка 9); гостиная-кухня — 24 мм (фартук: штукатурка 10 + клей 5 + плитка 9)); эти же грани — на развёртках и в раскладке плитки. Высоты — от чистого пола помещения.
2. Высоты и межосевые, отмеченные «*», приняты по практике монтажа; до черновой разводки сверить по паспорту выбранного прибора (смеситель, инсталляция, сифон).
3. Горячая вода (Т3) — слева от холодной (В1), если смотреть на прибор. Допуск установки выводов: ±5 мм в группе, ±20 мм у отдельно стоящих.
4. Расчёт систем водоснабжения и канализации и подбор оборудования выполняет проектная организация; лист задаёт места и высоты выводов.
5. Посудомоечная машина П4: кран и слив — отдельными выводами в шкафу мойки (не за машиной), до машины ≤ 1500 мм.
6. Прибор П3 мойка кухонная, П4 посудомоечная машина взят из расстановки мебели (по шкафу с мойкой).
7. Стояки в коробах/шахтах не замоноличивать; стояк К1 в коробе — звукоизоляция стояка в коробе без жёсткого контакта с трубой; к арматуре и ревизиям — люк не меньше 300×400.

1000 мм · печать 1:1

Изм.	Кол.уч	Лист	№ док.	Подп.	Дата
Разраб.		Кырлан А.С.			19.10.26
Пров.					
ГИП					
Н. контр.					
Утв.					

ГД-2026-012-АИ

Дом 120 м²

Общая площадь 147,36* м² · * размеры приняты, не замерены (реестр — л. 6, К-1)

Дизайн-проект интерьера

Стадия	Лист	Листов
РП	46	130

План выводов сантехники · 1-й этаж

М 1:40

Кырлан Александр Сергеевич

выпуск 19.10.2026 № 53e4f7ddae · стр. 50 из 160

План выводов сантехники · 2-й этаж

Выводы В1, Т3, К1 · привязки от чистовых стен · высоты от чистого пола, мм

ПРЕДВАРИТЕЛЬНО · не для производства работ · открыто пунктов: 6 (реестр — л. 6)

Фрагмент 1. Санузел второго этажа (пом. 13)

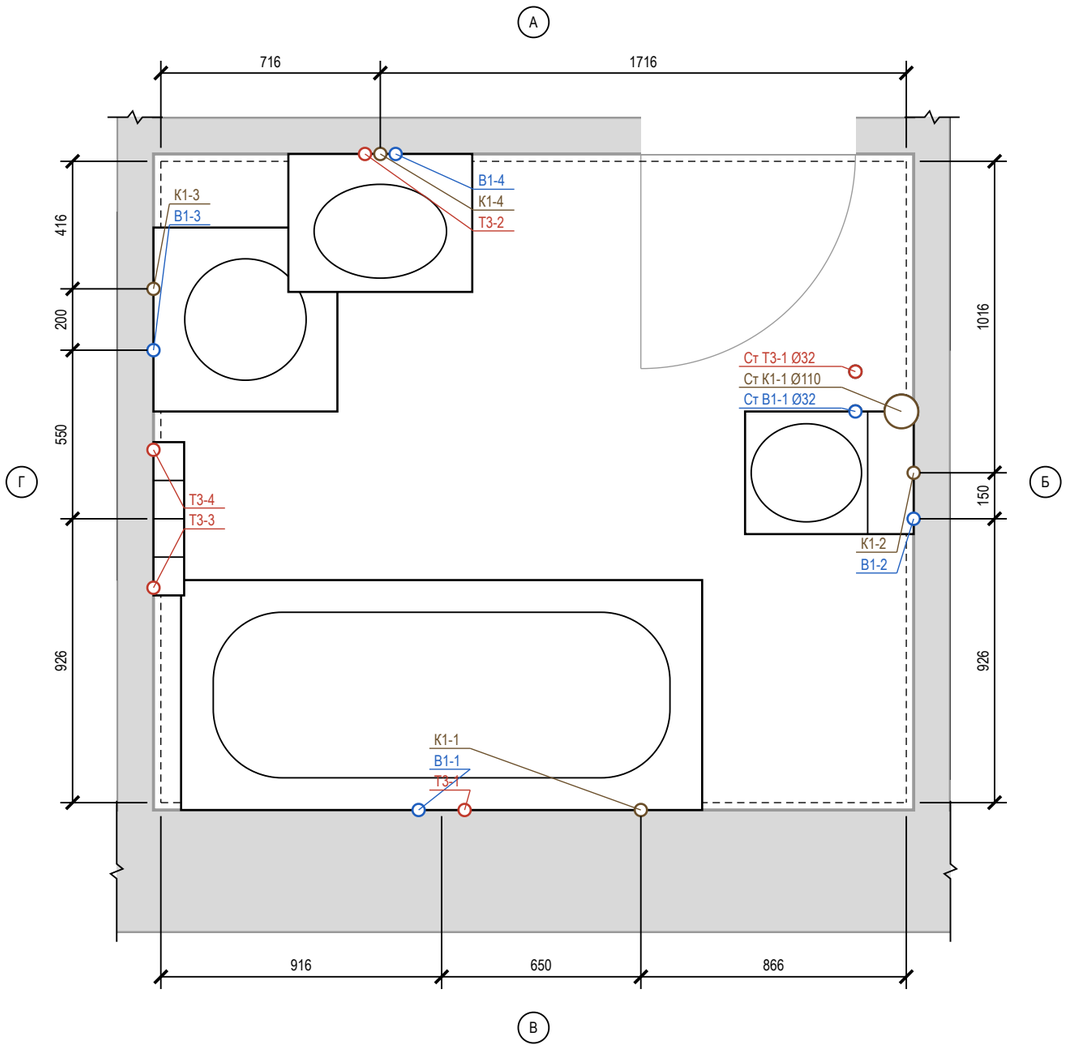

Ведомость привязок выводов

Код	Прибор	Ø	H, мм	Привязка от чист. стен, мм	Прим.
В1-1	См1 ванна	½"	800*	ст. В: 841 от Г	межос. 150
Т3-1	См1 ванна	½"	800*	ст. В: 991 от Г	межос. 150
К1-1	См1 ванна	Ø50	50*	ст. В: 866 от Б	
В1-2	См2 унитаз подвесной	½"	250*	ст. Б: 926 от В	в раме инсталляции
К1-2	См2 унитаз подвесной	Ø110	220*	ст. Б: 1016 от А	
В1-3	См3 стиральная машина	½"	600*	ст. Г: 616 от А	кран машины
К1-3	См3 стиральная машина	Ø50	600*	ст. Г: 416 от А	
В1-4	См4 умывальник	½"	600*	ст. А: 766 от Г	межос. 100
Т3-2	См4 умывальник	½"	600*	ст. А: 666 от Г	межос. 100
К1-4	См4 умывальник	Ø50	500*	ст. А: 716 от Г	
Т3-3	См5 полотенцесушитель	½"	1150*	ст. Г: 701 от В	подача, межос. 450; байпас и краны
Т3-4	См5 полотенцесушитель	½"	1150*	ст. Г: 941 от А	обратка

* — высота по практике монтажа; сверить по паспорту прибора

Условные обозначения

- вывод В1 (код — в ведомости привязок)
- вывод Т3 (код — в ведомости привязок)
- вывод К1 (код — в ведомости привязок)
- сантехприбор по расстановке (габарит модели)
- чистовая поверхность стены (от неё привязки)
- стояк «Ст К1-N / Ст В1-N» (ГОСТ 21.601), Ø мм
- линия обрыва (граница фрагмента)
- А — обозначение стены А–Г (как на развёртках)

Допущения и предложения на листе

Основа листа: взаимное расположение помещений, контур дома 9600 × 8000 и раскладка этажей подобраны проектировщиком под габариты помещений брифа; обмер и проект АР — задание (К-1); высота потолка 2900 мм — по брифу, не замерена; перекрытие 330 мм и отметка 2-го этажа +3,230 приняты; проект КР — задание (К-2); наружные стены 400 мм, перегородки 120 мм приняты (в брифе толщин нет) (К-1); разрешённая мощность 15 кВт принята по типовым ТУ для частного дома (К-4).
См. лист открытых вопросов (лист 6, записи К-1, К-2, К-4).

Примечания

1. Привязки выводов даны от чистовых поверхностей стен (облицовка на сторону: санузел второго этажа — 24 мм (штукатурка 10 + клей 5 + плитка 9)); эти же грани — на развёртках и в раскладке плитки. Высоты — от чистого пола помещения.
2. Высоты и межосевые, отмеченные «*», приняты по практике монтажа; до черновой разводки сверить по паспорту выбранного прибора (смеситель, инсталляция, сифон).
3. Горячая вода (Т3) — слева от холодной (В1), если смотреть на прибор. Допуск установки выводов: ±5 мм в группе, ±20 мм у отдельно стоящих.
4. Расчёт систем водоснабжения и канализации и подбор оборудования выполняет проектная организация; лист задаёт места и высоты выводов.
5. Стояки в коробах/шахтах не замоноличивать; стояк К1 в коробе — звукоизоляция стояка в коробе без жёсткого контакта с трубой; к арматуре и ревизиям — люк не меньше 300×400.

1000 мм · печать 1:1

Изм.	Кол.уч	Лист	№ док.	Подп.	Дата
Разраб.		Кырлан А.С.			19.10.26
Пров.					
ГИП					
Н. контр.					
Утв.					

ГД-2026-012-АИ

Дом 120 м²

Общая площадь 147,36* м² · * размеры приняты, не замерены (реестр — л. 6, К-1)

Дизайн-проект интерьера

Стадия	Лист	Листов
РП	47	130

План выводов сантехники · 2-й этаж

М 1:20

Кырлан Александр Сергеевич

выпуск 19.10.2026 № 53e4f7ddae · стр. 51 из 160

Схема разводки водопровода и канализации · 1-й этаж

Схемы систем В1, Т3, К1 · трассы принципиальные · уклоны в мм на 1 м · план М 1:200, фрагменты М 1:25

План квартиры (М 1:200)

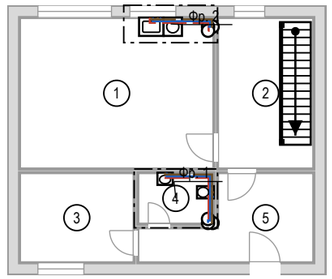

Допущения и предложения на листе

Основа листа: взаимное расположение помещений, контур дома 9600 × 8000 и раскладка этажей подобраны проектировщиком под габариты помещений брифа; обмер и проект АР — задание (К-1); высота потолка 2900 мм — по брифу, не замерена; перекрытие 330 мм и отметка 2-го этажа +3,230 приняты; проект КР — задание (К-2); наружные стены 400 мм, перегородки 120 мм приняты (в брифе толщин нет) (К-1); разрешённая мощность 15 кВт принята по типовым ТУ для частного дома (К-4).

Открытые вопросы и конфликты по листу: К-5, К-6.

См. лист открытых вопросов (лист 6, записи К-1, К-2, К-4–К-6).

Фр. 1. Санузел гостевой (М 1:25)

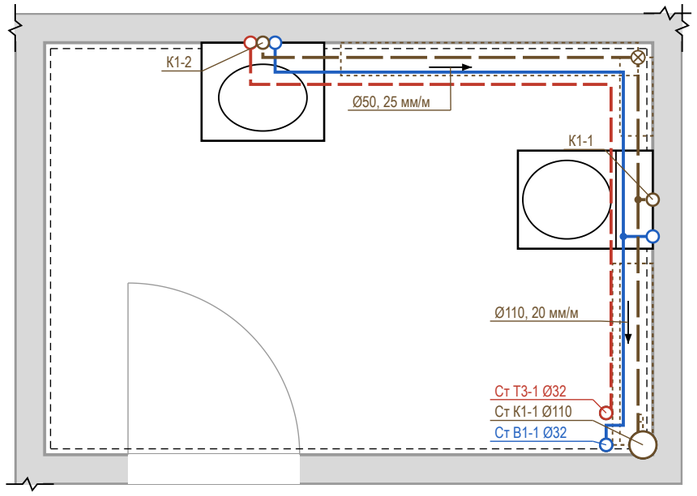

Фр. 2. Гостиная-кухня (М 1:25)

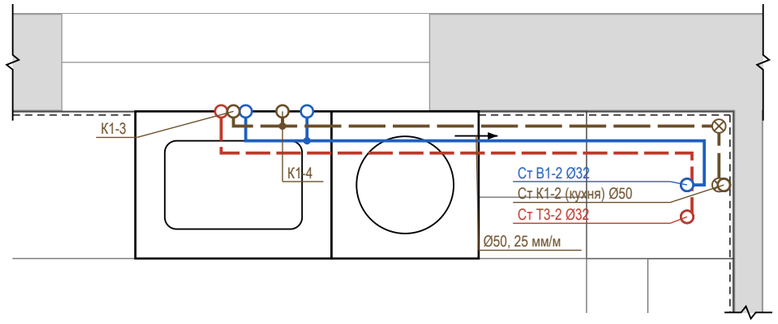

Условные обозначения

- В1 — водопровод хозяйственно-питьевой (ХВС), PP-R Ø20
- Т3 — горячее водоснабжение, подача (ГВС), PP-R Ø20
- К1 — канализация бытовая
- направление уклона К1 / пола: Ø, мм на 1 м
- ревизия (прочистка) К1 — доступ сохранить
- тройник (ответвление к прибору)
- короб К1 над чистым полом (ГКЛВ под плитку)
- вывод В1 (код — в ведомости привязок)
- вывод Т3 (код — в ведомости привязок)
- вывод К1 (код — в ведомости привязок)
- сантехприбор по расстановке (габарит модели)
- стояк «Ст К1-N / Ст В1-N» (ГОСТ 21.601), Ø мм
- линия обрыва (граница фрагмента)
- граница фрагмента на плане (Фр. N)

Профиль выпусков К1 (до врезки в стояк)

Выпуск	Прибор	Ø	L, м	i, мм/м	Δh, мм	Прокладка, мм
К1-1	Ст1 унитаз подвесной	Ø110	1,08	20	22	короб 170×140
К1-2	Ст2 умывальник	Ø50	3,19	25	80	короб 160×110
К1-3	П3 мойка кухонная	Ø50	2,30	25	58	над полом за приборами
К1-4	П4 посудомоечная машина	Ø40	2,10	30	63	над полом за приборами

Короб h×b: h — от чистого пола, b — от чистовой стены. Стяжка 35 мм — лист полов.

Узел ввода В1, Т3 (схема, без масштаба)

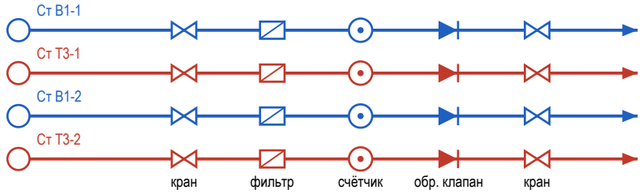

⊗ Ст К1-1, Ст К1-2 (кухня): ревизия на стояке — люк в коробе

Примечания

1. Трассы принципиальные, построены от стояков вдоль стен помещений; фактическое положение фиксируется исполнительной схемой с привязками (фото с рулеткой) до закрытия.
2. Уклон К1 не менее 1/d и не более 150 мм/м (СП 30.13330.2020, п. 19.1), приняты практические уклоны; поворот — двумя отводами 45°, ревизия после поворота, доступ сохранить. Стояк К1 в коробе — звукоизоляция стояка в коробе, без жёсткого контакта короба с трубой.
3. Решение по К1: стяжка 35 мм не укрывает трубы (нужно Ø + Δh + 45 мм) — выпуски идут над чистым полом вдоль стен: К1-3, К1-4 — за приборами и в раме инсталляции; К1-1, К1-2 — в коробе ГКЛВ под плитку (размеры в профиле). Короба — на развёртках; отметку низа врезки в стояк замерить до черновых работ.
4. На каждом вводе В1 и Т3 — кран шаровой, фильтр, счётчик, обратный клапан; доступ через люк не меньше 300×400. Водопровод — в штробе стен или в коробах; трубы испытать давлением до закрытия (акт скрытых работ).
5. Расчёт систем, диаметры магистралей и подбор оборудования выполняет проектная организация; врезка и перенос стояков — по согласованию с управляющей организацией. Арматуру и привязки сверить по паспортам приборов.

Изм.	Кол.уч	Лист	№ док.	Подп.	Дата
Разраб.		Кырлан А.С.			19.10.26
Пров.					
ГИП					
Н. контр.					
Утв.					

ГД-2026-012-АИ

Дом 120 м²

Общая площадь 147,36* м² · * размеры приняты, не замерены (реестр — л. 6, К-1)

Дизайн-проект интерьера

Стадия	Лист	Листов
РП	48	130

Схема разводки водопровода и канализации · 1-й этаж

М б/м

Кырлан Александр Сергеевич

выпуск 19.10.2026 № 53e477ddae · стр. 52 из 160

Схема разводки водопровода и канализации · 2-й этаж

Схемы систем В1, Т3, К1 · трассы принципиальные · уклоны в мм на 1 м · план М 1:200, фрагменты М 1:20

ПРЕДВАРИТЕЛЬНО · не для производства работ · открыто пунктов: 6 (реестр — л. 6)

План квартиры (М 1:200)

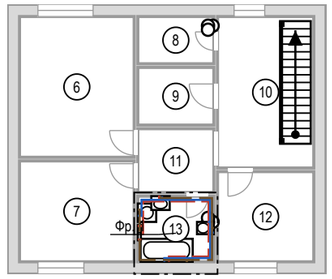

Фр. 1. Санузел второго этажа (М 1:20)

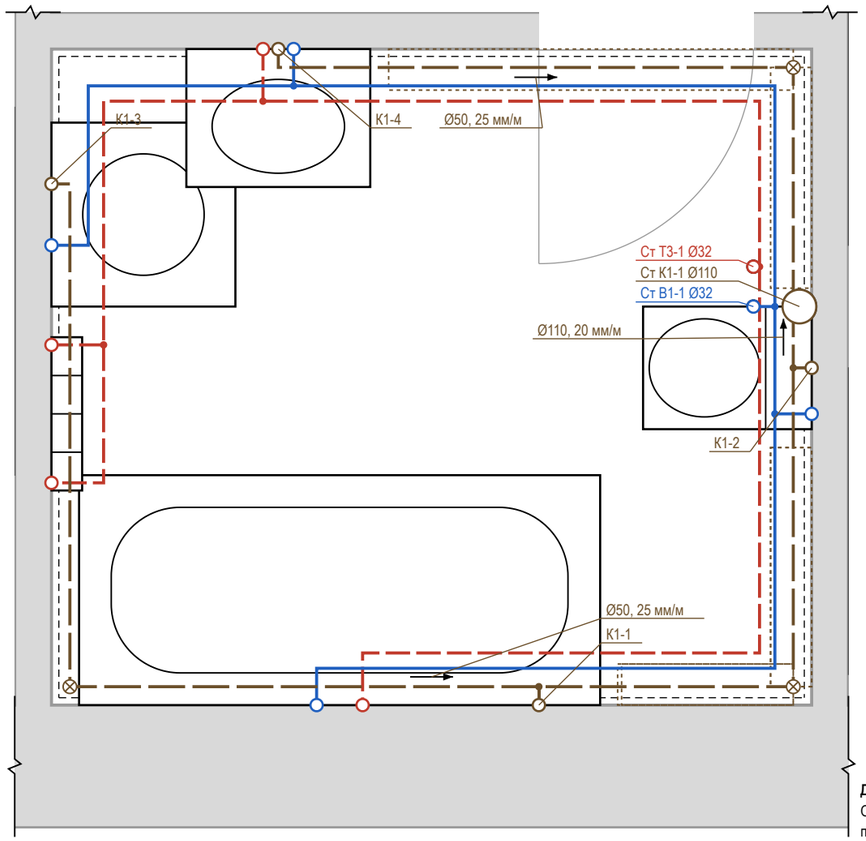

Условные обозначения

- В1 — водопровод хозяйственно-питьевой (ХВС), PP-R Ø20
- Т3 — горячее водоснабжение, подача (ГВС), PP-R Ø20
- К1 — канализация бытовая
- направление уклона К1 / пола: Ø, мм на 1 м
- ревизия (прочистка) К1 — доступ сохранить
- тройник (ответвление к прибору)
- короб К1 над чистым полом (ГКЛВ под плитку)
- вывод В1 (код — в ведомости привязок)
- вывод Т3 (код — в ведомости привязок)
- вывод К1 (код — в ведомости привязок)
- сантехприбор по расстановке (габарит модели)
- стояк «Ст К1-N / Ст В1-N» (ГОСТ 21.601), Ø мм
- линия обрыва (граница фрагмента)
- граница фрагмента на плане (Фр. N)

Профиль выпусков К1 (до врезки в стояк)

Выпуск	Прибор	Ø	L, м	i, мм/м	Δh, мм	Прокладка, мм
К1-2	См2 унитаз подвесной	Ø110	0,28	20	6	над полом за приборами
К1-3	См3 стиральная машина	Ø50	5,32	25	133	короб 220×110
К1-4	См4 умывальник	Ø50	2,54	25	64	под дверью — перенести выпуск
К1-1	См1 ванна	Ø50	2,15	25	54	короб 140×110

Короб h×b: h — от чистого пола, b — от чистовой стены. Стяжка 35 мм — лист полов.

Узел ввода В1, Т3 (схема, без масштаба)

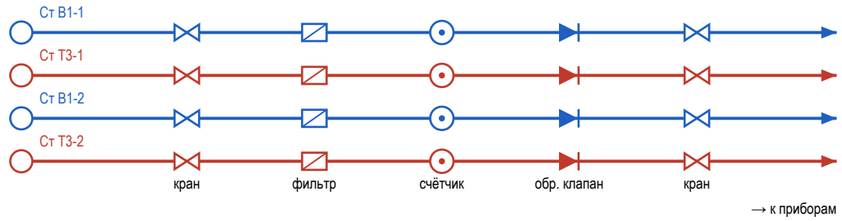

⊗ Ст К1-1, Ст К1-2 (кухня): ревизия на стояке — люк в коробе

Допущения и предложения на листе

Основа листа: взаимное расположение помещений, контур дома 9600 × 8000 и раскладка этажей подобраны проектировщиком под габариты помещений брифа; обмер и проект АР — задание (К-1); высота потолка 2900 мм — по брифу, не замерена; перекрытие 330 мм и отметка 2-го этажа +3,230 приняты; проект КР — задание (К-2); наружные стены 400 мм, перегородки 120 мм приняты (в брифе толщин нет) (К-1); разрешённая мощность 15 кВт принята по типовым ТУ для частного дома (К-4).

Открытые вопросы и конфликты по листу: К-5, К-6.

См. лист открытых вопросов (лист 6, записи К-1, К-2, К-4–К-6).

Примечания

1. Трассы принципиальные, построены от стояков вдоль стен помещений; фактическое положение фиксируется исполнительной схемой с привязками (фото с рулеткой) до закрытия.
2. Уклон К1 не менее 1/d и не более 150 мм/м (СП 30.13330.2020, п. 19.1), приняты практические уклоны; поворот — двумя отводами 45°, ревизия после поворота, доступ сохранить. Стояк К1 в коробе — звукоизоляция стояка в коробе, без жёсткого контакта короба с трубой.
3. Решение по К1: стяжка 35 мм не укрывает трубы (нужно Ø + Δh + 45 мм) — выпуски идут над чистым полом вдоль стен: К1-2 — за приборами и в раме инсталляции; К1-3, К1-4, К1-1 — в коробе ГКЛВ под плитку (размеры в профиле). Короба — на развёртках; отметку низа врезки в стояк замерить до черновых работ.
4. Трасса К1 от К1-4 проходит под дверным проёмом — короб там невозможен: выпуск перенести или вести в полу с подъёмом пола помещения.
5. На каждом вводе В1 и Т3 — кран шаровой, фильтр, счётчик, обратный клапан; доступ через люк не меньше 300×400. Водопровод — в штробе стен или в коробах; трубы испытать давлением до закрытия (акт скрытых работ).
6. Расчёт систем, диаметры магистралей и подбор оборудования выполняет проектная организация; врезка и перенос стояков — по согласованию с управляющей организацией. Арматуру и привязки сверить по паспортам приборов.

Изм.	Кол.уч	Лист	№ док.	Подп.	Дата
Разраб.		Кырлан А.С.			19.10.26
Пров.					
ГИП					
Н. контр.					
Утв.					

ГД-2026-012-АИ

Дом 120 м²

Общая площадь 147,36* м² · * размеры приняты, не замерены (реестр — л. 6, К-1)

Дизайн-проект интерьера	Стадия	Лист	Листов
	РП	49	130

Схема разводки водопровода и канализации · 2-й этаж
М б/м

Кырлан Александр Сергеевич

выпуск 19.10.2026 № 53e4f7ddae · стр. 53 из 160

Спецификация сантехнического оборудования

ПРЕДВАРИТЕЛЬНО · не для производства работ · открыто пунктов: 6 (реестр — л. 6)

Форма 1 ГОСТ 21.110-2013 · ГД-2026-012-АИ-ВК.СО · приборы, арматура, трубопроводы

Поз.	Наименование и техническая характеристика	Тип, марка, обозначение документа	Код продукции	Поставщик	Ед. изм.	Кол.	Масса 1 ед., кг	Примечание
	Санитарные приборы							
1	Ванна акриловая 1700×750 мм, с каркасом, экраном и отверстием слив-перелив	аналог		выбор заказчика	шт	1		См1
2	Унитаз подвесной безободковый, с сиденьем микролифт, крепёж и звукоизолирующая прокладка	Jacob Delafon Struktura EDF102-00		выбор заказчика	шт	2		Сг1, См2
3	Инсталляция для подвесного унитаза: рама высотой 1120 мм, бачок, клавиша смыва (ось клавиши 1050 мм от чистого пола)	аналог		выбор заказчика	шт	2		Сг1, См2; короб ГКЛВ
4	Умывальник подвесной 500×400 мм, с отверстием под смеситель и переливом	аналог		выбор заказчика	шт	1		Сг2
5	Умывальник подвесной 600×450 мм, с отверстием под смеситель и переливом	аналог		выбор заказчика	шт	1		См4
6	Мойка кухонная 800×600 мм, с переливом	аналог		с кухонной мебелью	шт	1		П8
7	Полотенцесушитель водяной (ГВС), с байпасом и кранами	аналог		выбор заказчика	шт	1		См5
	Смесители, сифоны и арматура приборов							
8	Смеситель для ванны настенный однорычажный, межосевое 150 мм, с душевым набором (лейка, шланг, держатель)	аналог		выбор заказчика	шт	1		См1
9	Смеситель для умывальника однорычажный, с донным клапаном	аналог		выбор заказчика	шт	2		Сг2, См4
10	Смеситель кухонный однорычажный, высокий излив	аналог		выбор заказчика	шт	1		П8
11	Обвязка ванны слив-перелив Ø40/50 с сифоном	аналог		выбор заказчика	шт	1		См1
12	Сифон для умывальника бутылочный Ø32/40–50, с гофрой к выпуску	аналог		выбор заказчика	шт	2		Сг2, См4
13	Сифон для мойки с отводом для ПММ Ø40/50	аналог		выбор заказчика	шт	1		П8
14	Сифон для стиральной машины встраиваемый в стену Ø50, с обратным клапаном	аналог		выбор заказчика	шт	1		См3
15	Кран угловой ½"×½" с гибкой подводкой 40 см (умывальники, мойка)	аналог		выбор заказчика	шт	6		по 2 на прибор
16	Кран шаровой угловой ½"×¾" для подключения стиральной и посудомоечной машины	аналог		выбор заказчика	шт	2		См3, П9
17	Узел подключения полотенцесушителя: байпас Ду20, краны шаровые ½" ×2	аналог		выбор заказчика	шт	1		
	Трубопроводы							
18	Труба полипропиленовая PP-R PN20 Ø20×3,4 (В1)	ГОСТ 32415-2013		выбор заказчика	м	18,5	0,17	12,3 + 4,3 + 10 %
19	Труба PP-R, армированная стекловолокном, PN20 Ø20×2,8 (Т3)	ГОСТ 32415-2013		выбор заказчика	м	19	0,15	12,0 + 4,9 + 10 %
20	Труба канализационная ПП Ø40 (К1)	ГОСТ 32414-2013		выбор заказчика	м	1		0,1 + 0,6 + 10 %
21	Труба канализационная ПП Ø50 (К1)	ГОСТ 32414-2013		выбор заказчика	м	12,5		9,3 + 2,0 + 10 %
22	Труба канализационная ПП Ø110 (К1)	ГОСТ 32414-2013		выбор заказчика	м	2		1,3 + 0,4 + 10 %
	Фасонные части и выводы							
23	Отвод канализационный ПП 45° Ø50	ГОСТ 32414-2013		выбор заказчика	шт	18		2 шт. на поворот
24	Отвод канализационный ПП 45° Ø110	ГОСТ 32414-2013		выбор заказчика	шт	6		2 шт. на поворот
25	Тройник канализационный ПП 45° (врезки ветвей)	ГОСТ 32414-2013		выбор заказчика	шт	7		
26	Ревизия канализационная ПП (после поворота трассы)	ГОСТ 32414-2013		выбор заказчика	шт	6		доступ сохранить
27	Фитинги PP-R Ø20: тройники, угольники 90° (ветви и повороты В1, Т3)	ГОСТ 32415-2013		выбор заказчика	шт	36		
28	Водорозетка PP-R Ø20×½" настенная, с креплением	ГОСТ 32415-2013		выбор заказчика	шт	14		коды — лист выводов
	Узлы ввода, люки, короба							
29	Кран шаровой латунный Ду15 PN16 (отключение ввода)	аналог		выбор заказчика	шт	4		Ст В1-1, Ст Т3-1, Ст В1-2, Ст Т3-2
30	Фильтр сетчатый косой Ду15	аналог		выбор заказчика	шт	4		
31	Счётчик воды крыльчатый Ду15 (ХВ, ГВ), с поверкой	аналог		выбор заказчика	шт	4		пломба УК
32	Клапан обратный Ду15	аналог		выбор заказчика	шт	4		
33	Люк ревизионный нажимной под плитку 300×400 мм	аналог		выбор заказчика	шт	2		к стоякам и арматуре
34	Звукоизоляция стояка К1 в коробе: рулонный звукоизоляционный материал ≥ 10 мм, обмотка стояка на высоту этажа	аналог		выбор заказчика	м	5,8		Ст К1-1, Ст К1-2 (кухня)
35	Короб К1 над полом: профиль ПН/ПС, ГКЛВ 12,5 мм под плитку	аналог		выбор заказчика	м	9,9		сечение — лист разводки

Примечания

1. Форма 1 ГОСТ 21.110-2013, ширины граф изменены по п. 4.1. «Аналог» — аналог по характеристикам: модели внести до черновых работ, привязки выводов сверить по паспортам.
2. Бытовая техника не входит (показана арматура подключения), мойка — в комплекте кухни. Длины труб — трасса листа разводки + подъёмы + 10 %.
3. Стояк К1 в коробе — звукоизоляция стояка в коробе без жёсткого контакта короба с трубой.
4. Расчёт систем водоснабжения и канализации, диаметры магистралей и подбор оборудования выполняет проектная организация.

Допущения и предложения на листе

Основа листа: взаимное расположение помещений, контур дома 9600 × 8000 и раскладка этажей подобраны проектировщиком под габариты помещений брифа; обмер и проект АР — задание (К-1); высота потолка 2900 мм — по брифу, не замерена; перекрытие 330 мм и отметка 2-го этажа +3,230 приняты; проект КР — задание (К-2); наружные стены 400 мм, перегородки 120 мм приняты (в брифе толщин нет) (К-1); разрешённая мощность 15 кВт принята по типовым ТУ для частного дома (К-4).
См. лист открытых вопросов (лист 6, записи К-1, К-2, К-4).

Изм.	Кол.уч	Лист	№ док.	Подп.	Дата
Разраб.		Кырлан А.С.			19.10.26
Пров.					
ГИП					
Н. контр.					
Утв.					

ГД-2026-012-АИ

Дом 120 м²

Общая площадь 147,36* м² · * размеры приняты, не замерены (реестр — л. 6, К-1)

Дизайн-проект интерьера

Стадия	Лист	Листов
РП	50	130

Спецификация сантехнического оборудования

М б/м

Кырлан Александр Сергеевич

Спецификация светильников и сценарии освещения

Светильники, ленты и блоки питания, слои света и сценарии по помещениям · б/м

Спецификация светильников

Поз.	Марки	Наименование	Установка	Кол.	P, Вт	Σ P, Вт	Ф, лм	Тц, К	Ra	Угол, °	IP	Дим.	Группа	Пом.
1	Св31–Св40	Встраиваемый точечный	встраиваемый	10	12	120	1000	3000	90	—	20	да	L12	1
2	Св41	Лента светодиодная 24 В	в коробе, профиль с рассеивателем	22,1 м	9,6/м	212,2	900/м	2700	90	—	20	да	L13	1
3	Св42**, Св43**, Св44**	Подвесной	подвес, низ H=1450	3	9	27	800	3000	90	—	20	да	L14	1
4	Св45–Св48	Встраиваемый точечный	встраиваемый	4	10	40	900	3000	90	—	20	да	L15	1
5	Св49**	Линейный настенный	под верхними шкафами, H=1440	1	18	18	1500	3000	90	—	20	да	L16	1
6	Св26–Св29, Св53, Св54, Св82–Св85	Встраиваемый точечный	встраиваемый	12	7	84	600	3000	90	—	20	—	L10, L84	2, 5, 10, 11
7	Св80	Подвесной	подвес	1	12	12	1100	3000	90	—	20	—	L80	2
8	Св17–Св22	Встраиваемый точечный	встраиваемый	6	14	84	1400	2700	90	—	20	—	L7	3
9	Св23	Лента светодиодная 24 В	в коробе, профиль с рассеивателем	12,3 м	9,6/м	118,1	900/м	2700	90	—	20	да	L8	3
10	Св50	Встраиваемый точечный	встраиваемый	1	7	7	600	3000	90	—	44	—	L17	4
11	Св12–Св14, Св51	Встраиваемый точечный	встраиваемый	4	6	24	500	3000	90	—	44	—	L4, L17	4, 13
12	Св15, Св52	Настенный светильник над зеркалом, драйвер встроен	над зеркалом, H=1900	2	8	16	600	3000	90	—	44	—	L5, L18	4, 13
13	Св30	Лента светодиодная 24 В	в коробе, профиль с рассеивателем, датчик движения	1,8 м	4,8/м	8,6	150/м	2700	90	—	20	нет	L11	5
14	Св1–Св8	Встраиваемый точечный	встраиваемый	8	12	96	1000	2700	90	—	20	—	L1	6
15	Св9	Лента светодиодная 24 В	в коробе, профиль с рассеивателем	15,5 м	9,6/м	148,8	900/м	2700	90	—	20	да	L2	6
16	Св10, Св11, Св24	Настенный (бра)	на стене, H=1500	4	6	24	400	2700	90	60	20	—	L3, L9	6, 7, 12
17	Св17–Св22	Встраиваемый точечный	встраиваемый	12	11	132	1100	2700	90	—	20	—	L7	7, 12
18	Св23	Лента светодиодная 24 В	в коробе, профиль с рассеивателем	24,6 м	9,6/м	236,2	900/м	2700	90	—	20	да	L8	7, 12
19	Св16	Потолочный накладной	на потолке, засветка стены	1	10	10	900	3000	90	—	20	—	L6	8
20	Св25	Потолочный накладной	на потолке	1	9	9	600	3000	90	—	20	—	L3	9
		Итого		**70 шт + 76,3 м**		**1426,8**								

LED-ленты, линейные светильники и блоки питания

Марка	Пом.	L, м	U, В	Вт/м	Σ P, Вт	БП	P БП, Вт	Загр., %	Питание	Доступ к БП
Св41	1	22,1	24	9,6	212,2	БП4	300	71	с двух концов	люк 300×300 в коробе У1 у входа
Св49**	1	3	24	—	18	БП5**	60	30	встроенный ввод	в пенале М6, верх, съёмная панель
Св23	3	12,3	24	9,6	118,1	БП2	200	177	с двух концов	люк 300×300 в коробе У1 у окна
Св30	5	1,8	24	4,8	8,6	БП3	20	43	с одного конца	в шкафу М16, верхняя полка
Св9	6	15,5	24	9,6	148,8	БП1	200	74	с двух концов	люк 300×300 в коробе У1 у входа
Св23	7	12,3	24	9,6	118,1	БП2	200	177	с двух концов	люк 300×300 в коробе У1 у окна
Св23	12	12,3	24	9,6	118,1	БП2	200	177	с двух концов	люк 300×300 в коробе У1 у окна

Сценарии освещения

Пом.	Сценарий	Группы и уровни, %	Чем включается
1	Вечер	L12 споты гостиной — 30; L13 подсветка короба — 100; L14 подвесы над столом — 50; L15 споты кухни — 0; L16 подсветка столешницы — 0	S10 светорегулятор, S11** светорегулятор
1	Ужин	L12 споты гостиной — 0; L13 подсветка короба — 60; L14 подвесы над столом — 100; L15 споты кухни — 0; L16 подсветка столешницы — 30	S10 светорегулятор, S11** светорегулятор, S12** светорегулятор
1	Кино	L12 споты гостиной — 0; L13 подсветка короба — 20; L14 подвесы над столом — 0; L15 споты кухни — 0; L16 подсветка столешницы — 0	S10 светорегулятор
1	Готовка	L12 споты гостиной — 50; L13 подсветка короба — 0; L14 подвесы над столом — 0; L15 споты кухни — 100; L16 подсветка столешницы — 100	S10 светорегулятор, S11** светорегулятор, S12** светорегулятор
3	Вечер	L7 споты — 0; L8 подсветка короба — 100; L9 бра — 100	S4, S5
6	Вечер	L1 споты — 0; L2 подсветка короба — 100; L3 бра — 100	S1, S2, S3
6	Уборка	L1 споты — 100; L2 подсветка короба — 100; L3 бра — 0	S1, S2, S3
7	Вечер	L7 споты — 0; L8 подсветка короба — 100; L9 бра — 100	S4, S5
12	Вечер	L7 споты — 0; L8 подсветка короба — 100; L9 бра — 100	S4, S5

Слои света

общий — равномерный свет помещения, по норме освещённости

рабочий — местный свет задачи: столешница, зеркало, чтение у кровати

акцентный — подсветка потолка, стен и ниш; не входит в поток общего света

ночной — путь спальня → санузел: не выше 2700 К, малая яркость, датчик движения

Допущения и предложения на листе

Основа листа: взаимное расположение помещений, контур дома 9600 × 8000 и раскладка этажей подобраны проектировщиком под габариты помещений брифа; обмер и проект АР — задание (К-1); высота потолка 2900 мм — по брифу, не замерена; перекрытие 330 мм и отметка 2-го этажа +3,230 приняты; проект КР — задание (К-2); наружные стены 400 мм, перегородки 120 мм приняты (в брифе толщин нет) (К-1); разрешённая мощность 15 кВт принята по типовым ТУ для частного дома (К-4).

Знак «**» — предложение проектировщика, заказчиком не утверждено (согласовать с заказчиком): записи в реестре нет: S11, S12 — светорегулятор добавлен разработчиком проекта; Св42, Св43, Св44, Св49, БП5 — диммируемость добавлена разработчиком проекта под светорегуляторы S11 и S12.

См. лист открытых вопросов (лист 6, записи К-1, К-2, К-4).

Примечания

1. Позиции и марки Св — те же, что на плане освещения (лист «План освещения») и в ведомости светильников (лист 34); группы L — по плану выключателей (лист «План выключателей»).
2. Модели светильников не назначены: подбор по графам спецификации — поток, Тц, Ra, угол, IP и диммирование не хуже указанных, мощность не больше. IP 20 — сухие помещения.
3. Длина LED-ленты в карнизе — по линии карниза плана потолков (лист «План потолков»); Σ P = Вт/м × длина. Блок питания загружен не больше чем на 80 %; лента 24 В длиннее 10 м питается с двух концов; доступ к блоку питания — люк ревизии 300×300 мм или место, указанное в таблице.
4. Сценарии: уровень — доля максимальной яркости группы, %; 0 — группа выключена. Уровень ниже 100 % — только у групп на светорегуляторе (задний фронт, ТЕ) с диммируемыми драйверами и блоками питания.
5. Мощность и поток — по паспортам принятых изделий, Σ P — установленная мощность освещения. Оценка освещённости — на плане освещения; это не светотехнический расчёт.
6. Не поместилось строк таблиц: 13 — продолжение выпустить отдельным листом.

Изм.	Кол.уч	Лист	№ док.	Подп.	Дата
Разраб.		Кырлан А.С.			19.10.26
Пров.					
ГИП					
Н. контр.					
Утв.					

ГД-2026-012-АИ

Дом 120 м²

Общая площадь 147,36* м² · * размеры приняты, не замерены (реестр — л. 6, К-1)

Дизайн-проект интерьера

Стадия	Лист	Листов
РП	51	130

Спецификация светильников и сценарии освещения
М б/м

Кырлан Александр Сергеевич

выпуск 19.10.2026 № 53e4f7ddae · стр. 55 из 160

План потолков · 1-й этаж

Уровни и марки потолков, короба с подсветкой, ниши под шторы, люки, вырезы · отметки низа от ±0,000 чистого пола · размеры в мм

ПРЕДВАРИТЕЛЬНО · не для производства работ · открыто пунктов: 6 (реестр — л. 6)

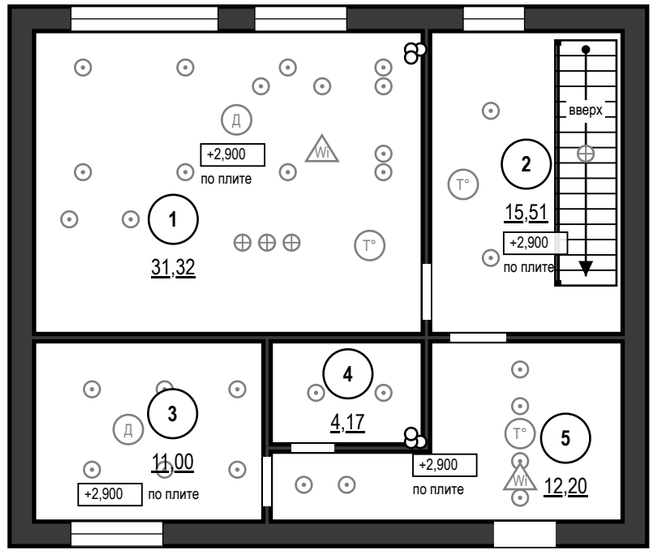

Ведомость потолков

Пом.	Марка	Конструкция	Низ	S, м²	Q
1		по плите, окраска	+2,900	31,32	
2		по плите, окраска	+2,900	15,51	
3		по плите, окраска	+2,900	11,00	
4		по плите, окраска	+2,900	4,17	
5		по плите, окраска	+2,900	12,20	
		Итого		**74,20**	

Ведомость вырезов и закладных в потолке

Марка	Устройство	Кол.	Пом.
	Светильник встраиваемый (марки — план освещения)	30	1, 2, 3, 4, 5
	Светильник подвесной (марки — план освещения)	4	1, 2
ИП4, ИП2	Извещатель дымовой	2	1, 3
ИП5, ИП6, ИП3	Извещатель тепловой	3	1, 2, 5
AP2**, AP1**	Точка доступа Wi-Fi, PoE	2	1, 5

Условные обозначения

- потолок по плите перекрытия, окраска, низ +2,900
- светильник встраиваемый — подложка с плана освещения
- светильник подвесной — подложка с плана освещения
- Д — извещатель дымовой на потолке — подложка
- T° — извещатель тепловой на потолке — подложка
- Wi — точка доступа Wi-Fi на потолке — подложка
- +2,6 — отметка низа потолка, м; под ней марка потолка
- 1 — номер помещения, площадь м²

Допущения и предложения на листе

Основа листа: взаимное расположение помещений, контур дома 9600 × 8000 и раскладка этажей подобраны проектировщиком под габариты помещений брифа; обмер и проект АР — задание (К-1); высота потолка 2900 мм — по брифу, не замерена; перекрытие 330 мм и отметка 2-го этажа +3,230 приняты; проект КР — задание (К-2); наружные стены 400 мм, перегородки 120 мм приняты (в брифе толщин нет) (К-1); разрешённая мощность 15 кВт принята по типовым ТУ для частного дома (К-4).

Знак «**» — предложение проектировщика, заказчиком не утверждено (согласовать с заказчиком): записи в реестре нет: AP2, AP1 — точка доступа Wi-Fi: число и места.

Открытые вопросы и конфликты по листу: К-2.

См. лист открытых вопросов (лист 6, записи К-1, К-2, К-4).

Примечания

1. За отметку ±0,000 принят уровень чистого пола сухих помещений (готовое покрытие), а не существующего пола; пол пом. 4 — −0,015; верх плиты перекрытия −0,064 — расчётный по пирогу пола, не замерен; существующий пол снимается до плиты, его отметка не замерена. Отметки в прямоугольниках — низ потолка; низ плиты перекрытия +2,900. Марка потолка — одна конструкция и отметка на весь альбом.
2. Светильники и потолочные устройства — подложка с планов освещения, слаботочных систем и вентиляции (положение — по ним); вырезы и закладные — по ведомости на листе, до обшивки; отверстия не совмещать с профилями.
3. Пом. 1, 2, 3, 4, 5 — потолок по плите без подвесной системы; отделка — по ведомости отделки.

1000 мм · печать 1:1

Изм.	Кол.уч	Лист	№ док.	Подп.	Дата
Разраб.		Кырлан А.С.			19.10.26
Пров.					
ГИП					
Н. контр.					
Утв.					

ГД-2026-012-АИ

Дом 120 м²

Общая площадь 147,36* м² · * размеры приняты, не замерены (реестр — л. 6, К-1)

Дизайн-проект интерьера

Стадия	Лист	Листов
РП	52	130

План потолков · 1-й этаж

М 1:100

Кырлан Александр Сергеевич

выпуск 19.10.2026 № 53e4f7ddae · стр. 56 из 160

План потолков · 2-й этаж

Уровни и марки потолков, короба с подсветкой, ниши под шторы, люки, вырезы · отметки низа от ±0,000 чистого пола · размеры в мм

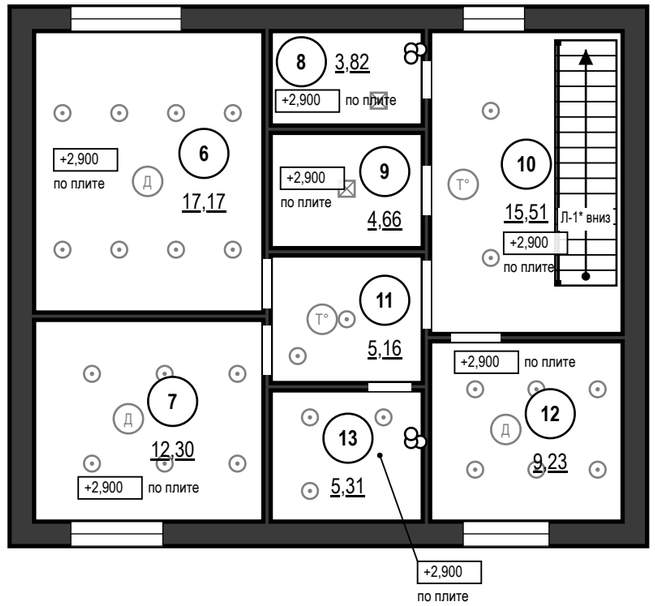

ПРЕДВАРИТЕЛЬНО · не для производства работ · открыто пунктов: 6 (реестр — л. 6)

Ведомость потолков

Пом.	Марка	Конструкция	Низ	S, м²	Q
6		по плите, окраска	+2,900	17,17	
7		по плите, окраска	+2,900	12,30	
8		по плите, окраска	+2,900	3,82	
9		по плите, окраска	+2,900	4,66	
10		по плите, окраска	+2,900	15,51	
11		по плите, окраска	+2,900	5,16	
12		по плите, окраска	+2,900	9,23	
13		по плите, окраска	+2,900	5,31	
		Итого		**73,16**	

Ведомость вырезов и закладных в потолке

Марка	Устройство	Кол.	Пом.
	Светильник встраиваемый (марки — план освещения)	27	6, 7, 10, 11, 12, 13
	Светильник накладной (марки — план освещения)	2	8, 9
ИП1, ИП2, ИП2	Извещатель дымовой	3	6, 7, 12
ИП6, ИП7	Извещатель тепловой	2	10, 11

Условные обозначения

- потолок по плите перекрытия, окраска, низ +2,900
- светильник встраиваемый — подложка с плана освещения
- светильник накладной — подложка с плана освещения
- Д — извещатель дымовой на потолке — подложка
- T° — извещатель тепловой на потолке — подложка
- +2,6 — отметка низа потолка, м; под ней марка потолка
- 1 — номер помещения, площадь м²

Допущения и предложения на листе

Основа листа: взаимное расположение помещений, контур дома 9600 × 8000 и раскладка этажей подобраны проектировщиком под габариты помещений брифа; обмер и проект АР — задание (К-1); высота потолка 2900 мм — по брифу, не замерена; перекрытие 330 мм и отметка 2-го этажа +3,230 приняты; проект КР — задание (К-2); наружные стены 400 мм, перегородки 120 мм приняты (в брифе толщин нет) (К-1); разрешённая мощность 15 кВт принята по типовым ТУ для частного дома (К-4).

Знак «*» — принято, не замерено и не подтверждено (замерить на объекте): К-3: Л-1 — место, тип и размеры лестницы брифом не заданы (только «лестница из холла 1-го этажа»): одномаршевая 17 × 190 × 250 вдоль стены Б холла — предложение проектировщика; конструкция и расчёт — проект КР.

Открытые вопросы и конфликты по листу: К-2.

См. лист открытых вопросов (лист 6, записи К-1–К-4).

Примечания

1. За отметку ±0,000 принят уровень чистого пола сухих помещений (готовое покрытие), а не существующего пола; пол пом. 13 — −0,015; верх плиты перекрытия −0,064 — расчётный по пирогу пола, не замерен; существующий пол снимается до плиты, его отметка не замерена. Отметки в прямоугольниках — низ потолка; низ плиты перекрытия +2,900. Марка потолка — одна конструкция и отметка на весь альбом.
2. Светильники и потолочные устройства — подложка с планов освещения, слаботочных систем и вентиляции (положение — по ним); вырезы и закладные — по ведомости на листе, до обшивки; отверстия не совмещать с профилями.
3. Пом. 6, 7, 8, 9, 10, 11, 12, 13 — потолок по плите без подвесной системы; отделка — по ведомости отделки.

1000 мм · печать 1:1

Изм.	Кол.уч	Лист	№ док.	Подп.	Дата
Разраб.		Кырлан А.С.			19.10.26
Пров.					
ГИП					
Н. контр.					
Утв.					

ГД-2026-012-АИ

Дом 120 м²

Общая площадь 147,36* м² · * размеры приняты, не замерены (реестр — л. 6, К-1)

Дизайн-проект интерьера

Стадия	Лист	Листов
РП	53	130

План потолков · 2-й этаж

М 1:100

Кырлан Александр Сергеевич

выпуск 19.10.2026 № 536477ddae · стр. 57 из 160

Раскладка плитки. Планы полов

Раскладка от чистовых размеров · размеры в мм · отметки от ±0,000

ПРЕДВАРИТЕЛЬНО · не для производства работ · открыто пунктов: 6 (реестр — л. 6)

Фрагмент 1. Санузел гостевой (пом. 4). Пол 600×600, шов 2 мм, М 1:25

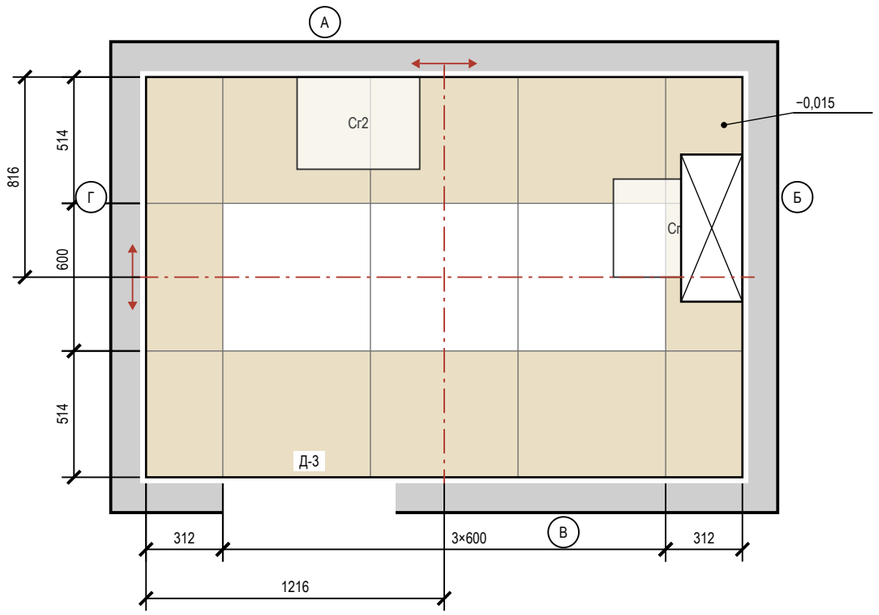

Фрагмент 2. Санузел второго этажа (пом. 13). Пол 600×600, шов 2 мм, М 1:25

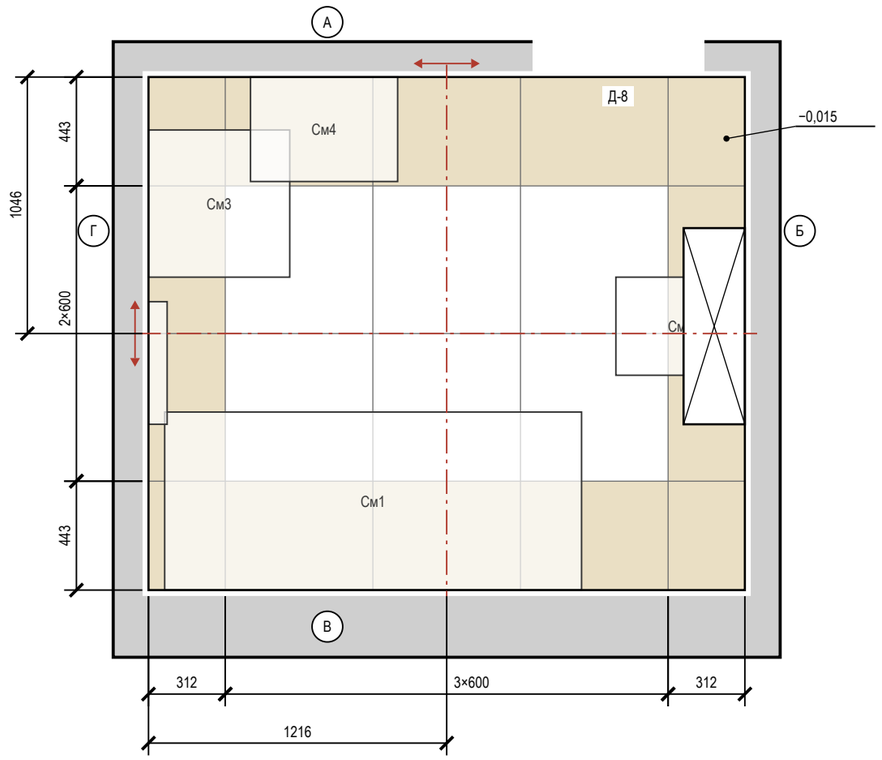

Примечания

1. Раскладка от чистовых размеров: стены санузлов теряют 10 + 5 + 9 = 24 мм на сторону (штукатурка, клей, плитка); подрезки чистые, без шва.
2. Старт — от центра помещения (штрихпунктир, стрелки направление укладки); размер старта — от чистовых стен Г и А.
3. Раскладка пола «Прихожая» и фартука «Гостиная-кухня» и фартука «Гостиная-кухня» — на листе «Раскладка плитки. Прихожая. Фартук кухни».
4. Калибр партии не задан — до укладки замерить (рабочий размер W, ГОСТ 13996-2019) и пересчитать подрезки.
5. Количество: целые по раскладке + по одной на подрезку, запас 10 %; один артикул — одна партия и тон. Исключены поддон, короб, проёмы и места за коробом; S — по чистым граням: стены нетто = зона облицовки по ведомости отделки − место за коробом инсталляции 1,68 м² (плитку за коробом не кладут), короб отдельной строкой.
6. Клей C2 TE S1 Ceresit CM 17; C2 TE S1 (ГОСТ Р 56387-2018), затирка CG2WA Mapei Ultracolor Plus 132; CG2WA; расход — по ТУ выбранной марки.
7. Гидроизоляция: пол и стены 200 мм от ЧП; над ванной — до 2000 и 300 мм за борт (см. развёртки); акт скрытых работ, пролив 24 ч.
8. Швы пола совмещены со швами стены А; по периметру — демпферная лента.
9. Отметка чистого пола −0,015, порог 15 мм; стык с соседним покрытием — по оси полотна двери.

Условные обозначения

- плитка целая; тонкая линия — шов
- плитка с подрезкой (размер — на цепочке)
- ось старта; стрелки — направление укладки
- сантехприбор: габарит, высота по практике
- короб инсталляции: плитка пола — до короба
- отметка чистого пола на полке выноски, м
- (А) обозначение стены А–Г (как на развёртках)

Допущения и предложения на листе

Основа листа: взаимное расположение помещений, контур дома 9600 × 8000 и раскладка этажей подобраны проектировщиком под габариты помещений брифа; обмер и проект АР — задание (К-1); высота потолка 2900 мм — по брифу, не замерена; перекрытие 330 мм и отметка 2-го этажа +3,230 приняты; проект КР — задание (К-2); наружные стены 400 мм, перегородки 120 мм приняты (в брифе толщин нет) (К-1); разрешённая мощность 15 кВт принята по типовым ТУ для частного дома (К-4).
См. лист открытых вопросов (лист 6, записи К-1, К-2, К-4).

Ведомость плитки

Помещение, поверхность	Плитка, код	Формат	Шов	S, м²	Целых	Подр.	С запасом
Санузел гостевой, пол	аналог: керамогранит под травертин	600×600	2	4,17	3	12	17
Санузел гостевой, стены А–Г	аналог: керамогранит под травертин	600×1200	2	16,68	11	21	36
Санузел гостевой, короб инсталляции	аналог: керамогранит под травертин	600×1200	2	1,47	1	3	5
Санузел второго этажа, пол	аналог: керамогранит под травертин	600×600	2	5,31	6	14	22
Санузел второго этажа, стены А–Г	аналог: керамогранит под травертин	600×1200	2	18,10	16	20	40
Санузел второго этажа, короб инсталляции	аналог: керамогранит под травертин	600×1200	2	1,76	0	6	7
Прихожая, пол	A8UZ	600×1200	2	12,20	4	14	20
Гостиная-кухня, фартук (ст. А)	аналог: керамогранит под травертин, матовый	1200×600	2	0,65	0	3	4
Гостиная-кухня, фартук (ст. Б)	аналог: керамогранит под травертин, матовый	1200×600	2	1,35	0	2	3
Итого 600×600				9,48	9	26	39
Итого 600×1200				**52,21**	**32**	**69**	**115**

Ведомость материалов

Материал	Класс, код	Норма расхода	Кол-во
Затирка	CG2WA Mapei Ultracolor Plus 132	(a+b)/ab·шов·t·1,6	4,1 кг
Затирка	CG2WA	(a+b)/ab·шов·t·1,6	0,9 кг
Клей	C2 TE S1 Ceresit CM 17	1,5 кг/м²·мм, слой 5	402 кг (17 меш.)
Клей	C2 TE S1	1,5 кг/м²·мм, слой 5	92 кг (4 меш.)
Гидроизоляция	обмазочная, 2 слоя: пол, стены по периметру и зоны замачивания	по ТУ	19,6 м²
Демпф. лента	по периметру пола из плитки		27,6 м

1000 мм · печать 1:1

Изм.	Кол.уч	Лист	№ док.	Подп.	Дата
Разраб.		Кырлан А.С.			19.10.26
Пров.					
ГИП					
Н. контр.					
Утв.					

ГД-2026-012-АИ

Дом 120 м²

Общая площадь 147,36* м² · * размеры приняты, не замерены (реестр — л. 6, К-1)

Дизайн-проект интерьера

Стадия	Лист	Листов
РП	54	130

Раскладка плитки. Планы полов

М 1:25

Кырлан Александр Сергеевич

выпуск 19.10.2026 № 53e4f7ddae · стр. 58 из 160

Раскладка плитки. Прихожая. Фартук кухни

Раскладка от чистовых размеров · размеры в мм · высоты фартука от чистого пола

ПРЕДВАРИТЕЛЬНО · не для производства работ · открыто пунктов: 6 (реестр — л. 6)

Фрагмент 1. Прихожая (пом. 5). Пол 600×1200, шов 2 мм, М 1:25

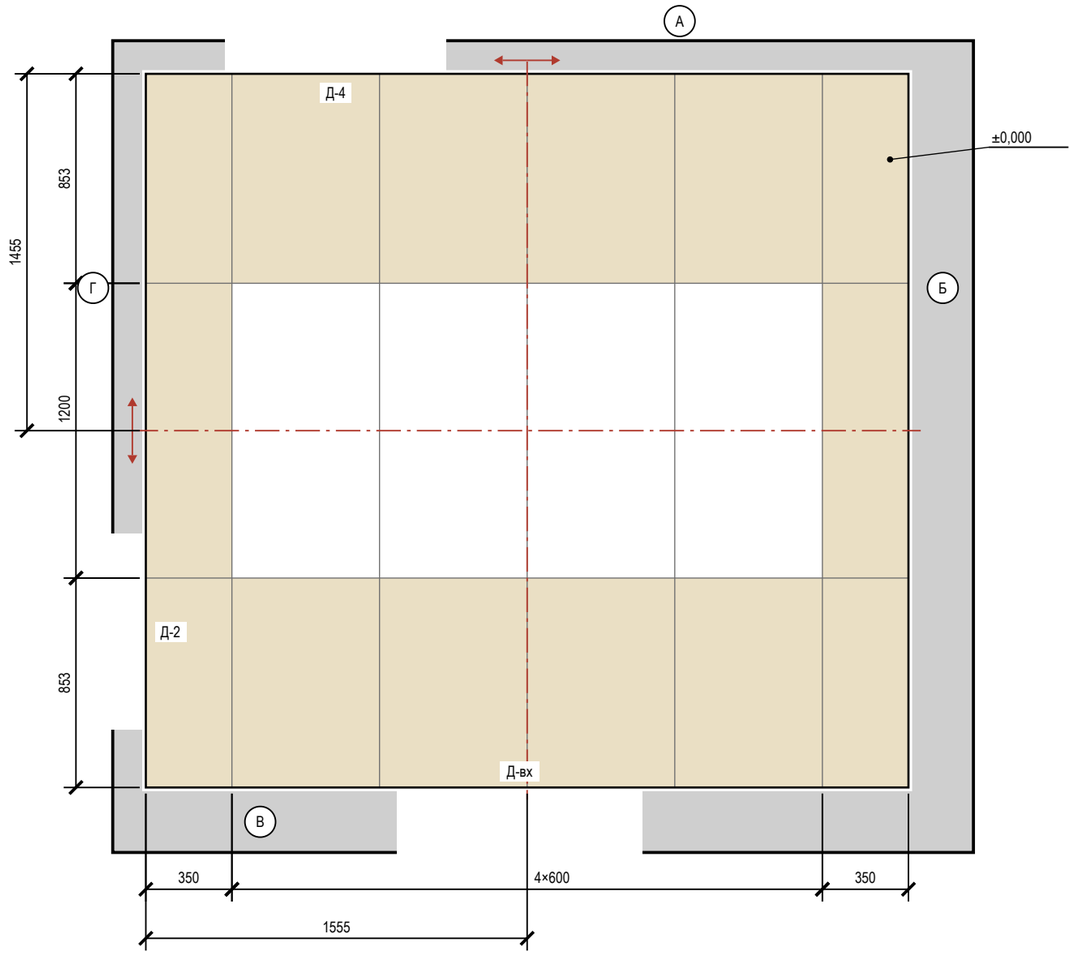

Фрагмент 2. Гостиная-кухня (пом. 1), фартук, стена А. 1200×600, шов 2 мм, М 1:25

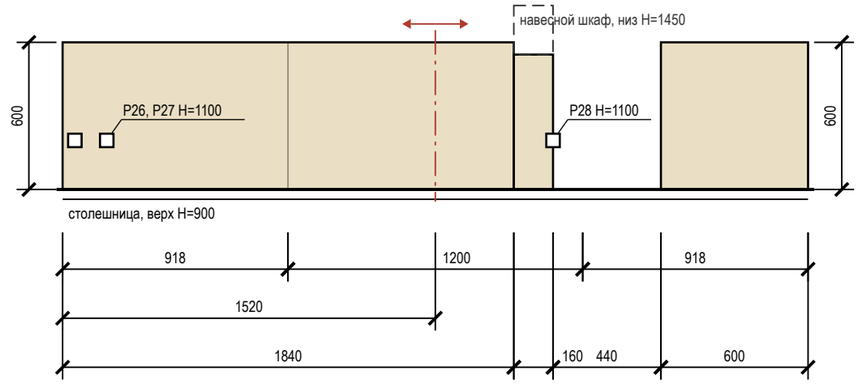

Фрагмент 3. Гостиная-кухня (пом. 1), фартук, стена Б. 1200×600, шов 2 мм, М 1:25

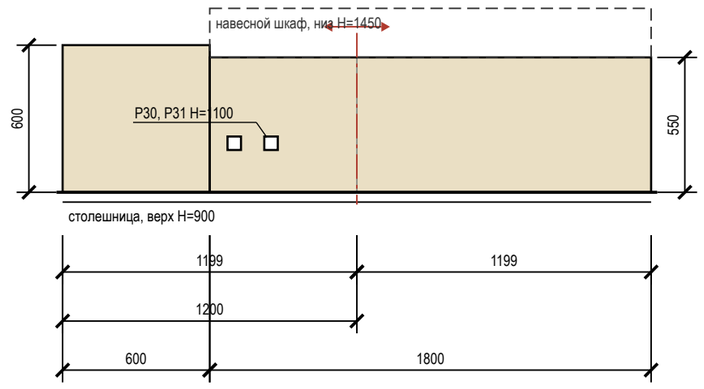

Условные обозначения

- плитка целая; тонкая линия — шов
- плитка с подрезкой (размер — на цепочке)
- ось старта; стрелки — направление укладки
- электроточка: марка и Н — по листам ЭОМ
- столешница (верх)
- навесной шкаф над фартуком
- отметка чистого пола на полке выноски, м
- А — обозначение стены А–Г (как на развёртках)

Подсчёт плитки

Поверхность	Формат	S, м²	Целых	Подр.	С запасом
Прихожая, пол	600×1200	12,20	4	14	20
Гостиная-кухня, фартук (ст. А)	1200×600	0,65	0	3	4
Гостиная-кухня, фартук (ст. Б)	1200×600	1,35	0	2	3

Сдвиг розеток фартука под раскладку

Точка (ЭОМ)	Проект: от угла / Н	Под раскладку: от угла / Н	Сдвиг, мм
P26, P27	50, 180 / 1100	50, 180 / 1200	Н +100 — ось ряда
P28	2000 / 1100	2000 / 1175	Н +75 — ось ряда
P30, P31	700, 850 / 1100	700, 850 / 1175	Н +75 — ось ряда

1000 мм · печать 1:1

Примечания

1. Прихожая: керамогранит 600×1200, длинная сторона — вдоль стен Б и Г, шов 2 мм, прямая раскладка от центра. Стены окрашены: раскладка от чистового контура минус штукатурка и шпаклёвка 15 мм на сторону (принято); подрезки 350 / 853 мм, срез — под плинтус.
2. Прихожая: деформационный зазор по периметру 8–10 мм под плинтусом; в проёмах — стык с соседним покрытием по оси полотна двери. Клей С2 TE S1, затирка CG2WA.
3. Фартук, Гостиная-кухня: 1200×600 горизонтально, шов 2 мм; зоны 1840 мм — 900…1500, 160 мм — 900…1450, 600 мм — 900…1500 (от столешницы до низа навесного шкафа, без шкафа — 600 мм). Старт от центра участка, подрезки 918 мм. Площадь 0,65 м² — как в ведомости отделки.
4. Фартук — после монтажа столешницы, низ на 2–3 мм выше неё, шов со столешницей — санитарный герметик; навесные шкафы — после фартука. Торцы у пенала и стены — профиль или запил 45°.
5. Фартук, Гостиная-кухня: 1200×600 горизонтально, шов 2 мм; зоны 600 мм — 900…1500, 1800 мм — 900…1450 (от столешницы до низа навесного шкафа, без шкафа — 600 мм). Старт от центра участка, подрезки нет мм. Площадь 1,35 м² — как в ведомости отделки.
6. Фартук — после монтажа столешницы, низ на 2–3 мм выше неё, шов со столешницей — санитарный герметик; навесные шкафы — после фартука. Торцы у пенала и стены — профиль или запил 45°.
7. Розетки из таблицы переносятся до черновой электрики: по высоте — на ось ряда плитки, от вертикального шва крупной плитки — не ближе 60 мм. Привязка — от левого края фартука на развёртке.
8. Клей, затирка и итог по форматам — в ведомостях листа «Раскладка плитки. Планы полов».

Допущения и предложения на листе

Основа листа: взаимное расположение помещений, контур дома 9600 × 8000 и раскладка этажей подобраны проектировщиком под габариты помещений брифа; обмер и проект АР — задание (К-1); высота потолка 2900 мм — по брифу, не замерена; перекрытие 330 мм и отметка 2-го этажа +3,230 приняты; проект КР — задание (К-2); наружные стены 400 мм, перегородки 120 мм приняты (в брифе толщин нет) (К-1); разрешённая мощность 15 кВт принята по типовым ТУ для частного дома (К-4).
Знак «**» — предложение проектировщика, заказчиком не утверждено (согласовать с заказчиком): записи в реестре нет: плинтус пом. 1, 5, фартук пом. 1 — артикул изделия не выбран: позиция описана характеристиками («аналог по характеристикам»), артикул выбирается при закупке.
См. лист открытых вопросов (лист 6, записи К-1, К-2, К-4).

Изм.	Кол.уч	Лист	№ док.	Подп.	Дата
Разраб.		Кырлан А.С.			19.10.26
Пров.					
ГИП					
Н. контр.					
Утв.					

ГД-2026-012-АИ

Дом 120 м²

Общая площадь 147,36* м² · * размеры приняты, не замерены (реестр — л. 6, К-1)

Дизайн-проект интерьера

Стадия	Лист	Листов
РП	55	130

Раскладка плитки. Прихожая. Фартук кухни

М 1:25

Кырлан Александр Сергеевич

выпуск 19.10.2026 № 53e4f7ddae · стр. 59 из 160

Раскладка плитки. Санузел гостевой. Развёртки стен

ПРЕДВАРИТЕЛЬНО · не для производства работ · открыто пунктов: 6 (реестр — л. 6)

Пом. 4 · вид изнутри помещения · размеры в мм · высоты от чистого пола, отметки от ±0,000

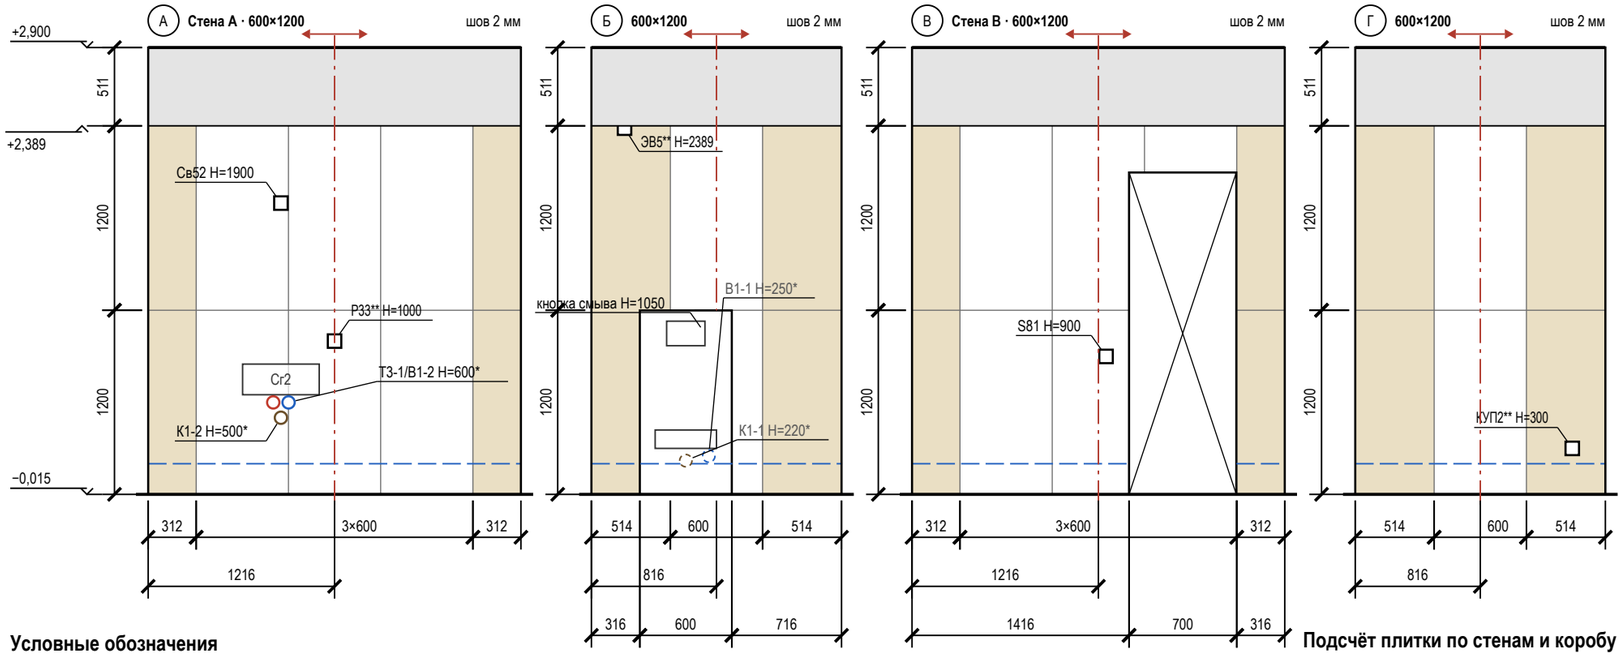

Условные обозначения

- плитка целая; тонкая линия — шов
- плитка с подрезкой (размер — на цепочке)
- ось старта; стрелки — направление укладки
- верх гидроизоляции: 200 от ЧП, в мокрой зоне — «до …»
- проём — не облицовывается
- сантехприбор: габарит, высота по практике
- короб инсталляции, в нём кнопка смыва 250×160
- вывод В1 (код — в ведомости привязок)
- вывод Т3 (код — в ведомости привязок)
- вывод К1 (код — в ведомости привязок)
- вывод за прибором / в коробе (не на сетке)
- электроточка: марка и Н — по листам ЭОМ
- отметка уровня, м: ±0,000 — чистый пол жилых помещений
- низ потолка; серая полоса — стена без плитки
- (А) обозначение стены А–Г (как на развёртках)

Подсчёт плитки по стенам и коробу

Поверхность	L × H, мм	S, м²	Целых	Подр.	С запасом	Подрезки: край / верх, мм
стена А	2432 × 2404	5,96	6	4	11	312 / 312; целый ряд
стена Б	1632 × 2404	3,32	1	5	7	514 / 514; целый ряд
короб (ст. Б)	600×1200×250	1,47	1	3	5	лицо 600; бок. 250
стена В	2432 × 2404	4,49	2	8	11	312 / 312; целый ряд
стена Г	1632 × 2404	2,90	2	4	7	514 / 514; целый ряд
Итого		**18,15**	**12**	**24**	**41**	

Сдвиг точек под раскладку

Точка (ВК, ЭОМ)	Стена	Проект: от угла / Н	Под раскладку: от угла / Н	Сдвиг, мм
Т3-1/В1-2, К1-2, Св52	А	866 / 600, 500, 1900	915 / 600, 500, 1900	+49 на шов
ЭВ5**	Б	216 / 2389	216 / 2403	Н +14
S81	В	1266 / 900	1216 / 900	−50 в центр плитки

Допущения и предложения на листе

Основа листа: взаимное расположение помещений, контур дома 9600 × 8000 и раскладка этажей подобраны проектировщиком под габариты помещений брифа; обмер и проект АР — задание (К-1); высота потолка 2900 мм — по брифу, не замерена; перекрытие 330 мм и отметка 2-го этажа +3,230 приняты; проект КР — задание (К-2); наружные стены 400 мм, перегородки 120 мм приняты (в брифе толщин нет) (К-1); разрешённая мощность 15 кВт принята по типовым ТУ для частного дома (К-4).

Знак «**» — предложение проектировщика, заказчиком не утверждено (согласовать с заказчиком): записи в реестре нет: Р33 — по образцу: Розетка Р33 на высоте 1100 мм, вне шва плитки; ЭВ5, КУП2 — по образцу: Добавлены выводы к вентиляторам: ЭВ4 (ВР1, ванная) и ЭВ5 (ВР3, санузел 2) — группа 3, высота 2389 мм, включение с основным светом, таймер выбега в вентиляторе; и коробки уравнивания потенциалов КУП1 (ванная) и КУП2 (санузел 2) — высота 300 мм, у входа, вне зон 0–2, проводник от шины РЕ щита ЩК, сече.

См. лист открытых вопросов (лист 6, записи К-1, К-2, К-4).

Примечания

1. Вид изнутри, стены по часовой стрелке А → Г. Высоты — от чистого пола (−0,015), отметки — от ±0,000. Раскладка от чистовых размеров (штукатурка 10 + клей 5 + плитка 9 мм), подрезки чистые; старт — от оси стены, ряды от пола целыми.
2. Верх плитки +2,389, потолок +2,900, зазор 511 мм: потолок ГКЛ опустить до +2,392 (шов 3 мм, герметик) — согласовать с монтажником ГКЛ; иначе профиль-окантовка, полосу окрасить в цвет потолка. Подрезной ряд 506 мм не делать.
3. Точки из таблицы сдвигов переносятся до черновой разводки: смеситель — по оси пары В1 + Т3; вывод на оси прибора — вместе с прибором, иначе старт раскладки — на ось прибора.
4. Выводы — по «Плану выводов сантехники», электроточки — по ЭОМ, «*» — высота по практике; за приборами и в коробе (В1-1, К1-1) — штриховым кольцом.
5. Гидроизоляция: 200 мм от ЧП по периметру; углы — лентой; акт скрытых работ, пролив.
6. Короб 600×1200×250: лицо 600 мм от оси кнопки смыва, боковины, полка; углы — запил 45° или профиль; за коробом плитку не кладут.
7. Линии узора (швы плитки, складки штор, рёбра радиаторов) прерываются у знаков и выносок — просвет между линиями не менее 0,7 мм.

1000 мм · печать 1:1

Изм.	Кол.уч	Лист	№ док.	Подп.	Дата
Разраб.		Кырлан А.С.			19.10.26
Пров.					
ГИП					
Н. контр.					
Утв.					

ГД-2026-012-АИ

Дом 120 м²

Общая площадь 147,36* м² · * размеры приняты, не замерены (реестр — л. 6, К-1)

Дизайн-проект интерьера

Стадия	Лист	Листов
РП	56	130

Раскладка плитки. Санузел гостевой. Развёртки стен

М 1:40

Кырлан Александр Сергеевич

выпуск 19.10.2026 № 53e4f7ddae · стр. 60 из 160

Раскладка плитки. Санузел второго этажа. Развёртки стен

Пом. 13 · вид изнутри помещения · размеры в мм · высоты от чистого пола, отметки от ±0,000

ПРЕДВАРИТЕЛЬНО · не для производства работ · открыто пунктов: 6 (реестр — л. 6)

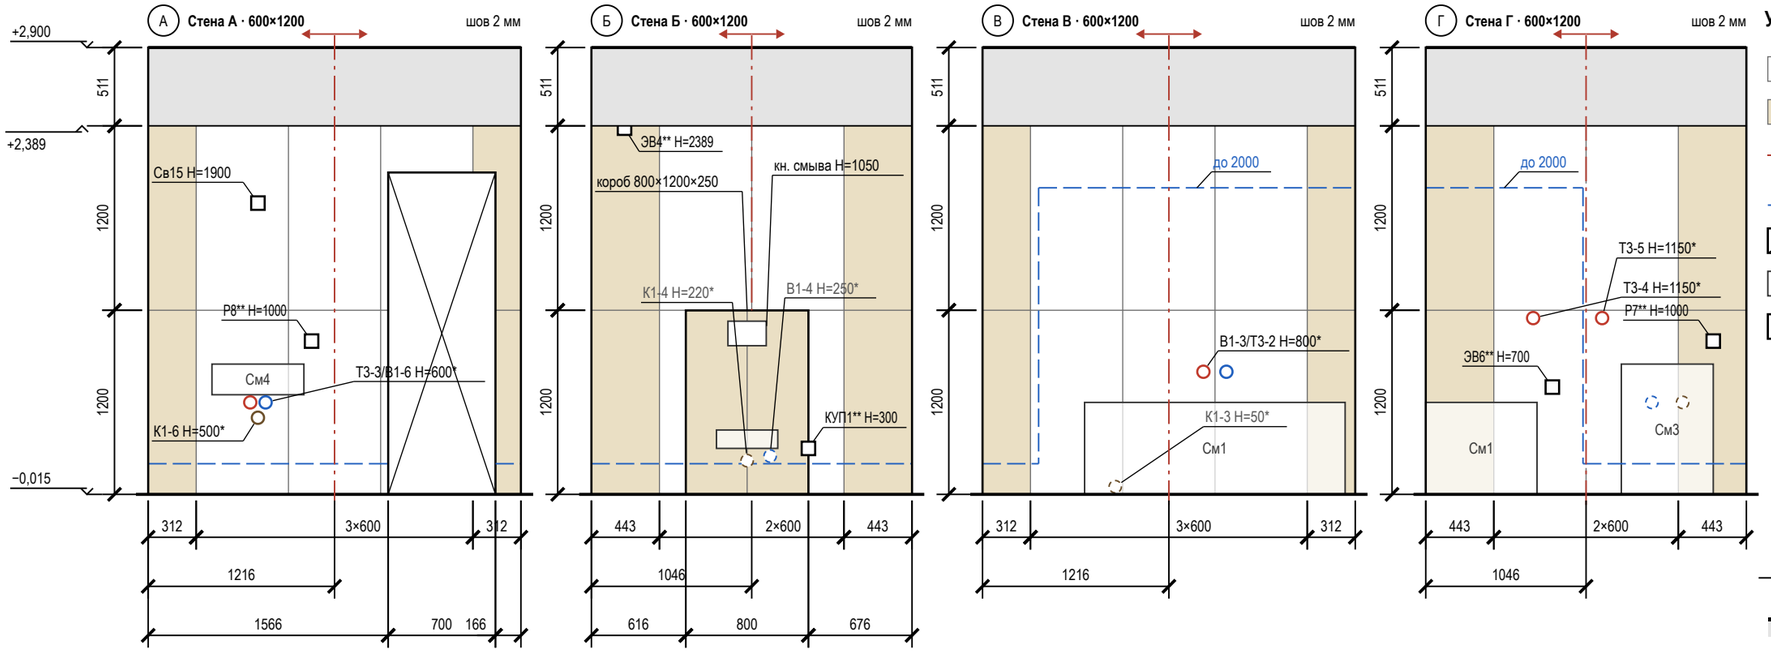

Условные обозначения

- плитка целая; тонкая линия — шов
- плитка с подрезкой (размер — на цепочке)
- ось старта; стрелки — направление укладки
- верх гидроизоляции: 200 от ЧП, в мокрой зоне — «до …»
- проём — не облицовывается
- сантехприбор: габарит, высота по практике
- короб инсталляции, в нём кнопка смыва 250×160
- вывод В1 (код — в ведомости привязок)
- вывод Т3 (код — в ведомости привязок)
- вывод К1 (код — в ведомости привязок)
- вывод за прибором / в коробе (не на сетке)
- электроточка: марка и Н — по листам ЭОМ
- отметка уровня, м: ±0,000 — чистый пол жилых помещений
- низ потолка; серая полоса — стена без плитки
- А — обозначение стены А–Г (как на развёртках)

Подсчёт плитки по стенам и коробу

Поверхность	L × H, мм	S, м²	Целых	Подр.	С запасом	Подрезки: край / верх, мм
стена А	2432 × 2404	4,49	4	6	11	312 / 312; целый ряд
стена Б	2092 × 2404	4,18	2	6	9	443 / 443; целый ряд
короб (ст. Б)	800×1200×250	1,76	0	6	7	лицо 399 / 399; бок. 250
стена В	2432 × 2404	5,96	6	4	11	312 / 312; целый ряд
стена Г	2092 × 2404	3,46	4	4	9	443 / 443; целый ряд
Итого		**19,86**	**16**	**26**	**47**	

Сдвиг точек под раскладку

Точка (ВК, ЭОМ)	Стена	Проект: от угла / Н	Под раскладку: от угла / Н	Сдвиг, мм
Т3-3/В1-6, К1-6, Св15	А	716 / 600, 500, 1900	614 / 600, 500, 1900	−102 в центр плитки
Р8**	А	1066 / 1000	1216 / 1000	+150 в центр плитки
ЭВ4**	Б	216 / 2389	143 / 2403	−73 в центр плитки; Н +14
КУП1**	Б	1416 / 300	1347 / 300	−69 в центр плитки
Т3-4	Г	701 / 1150	745 / 1150	+44 в центр плитки
Т3-5	Г	1151 / 1150	1046 / 1150	−105 на шов
Р7**	Г	1876 / 1000	1949 / 1000	+73 в центр плитки
ЭВ6**	Г	826 / 700	745 / 700	−81 в центр плитки

Примечания

1. Вид изнутри, стены по часовой стрелке А → Г. Высоты — от чистого пола (−0,015), отметки — от ±0,000. Раскладка от чистовых размеров (штукатурка 10 + клей 5 + плитка 9 мм), подрезки чистые; старт — от оси стены, ряды от пола целыми.
2. Верх плитки +2,389, потолок +2,900, зазор 511 мм: потолок ГКЛ опустить до +2,392 (шов 3 мм, герметик) согласовать с монтажником ГКЛ; иначе профиль-окантовка, полосу окрасить в цвет потолка. Подрезной ряд 506 мм не делать.
3. Точки из таблицы сдвигов переносятся до черновой разводки: смеситель — по оси пары В1 + Т3; вывод на ось прибора — вместе с прибором, иначе старт раскладки — на ось прибора.
4. Выводы — по «Плану выводов сантехники», электроточки — по ЭОМ, «*» — высота по практике; за приборами и в коробе (В1-4, К1-4, К1-3, В1-5, К1-5) — штриховым кольцом.
5. Гидроизоляция: 200 мм от ЧП по периметру; над ванной — до 2000 и 300 мм за борт (СП 29.13330.2011, п. 7.2 — на высоту замачивания); углы — лентой; акт скрытых работ, пролив.
6. Короб 800×1200×250: лицо 399 / 399 мм от оси кнопки смыва, боковины, полка; углы — запил 45° или профиль; за коробом плитку не кладут.
7. Линии узора (швы плитки, складки штор, рёбра радиаторов) прерываются у знаков и выносок — просвет между линиями не менее 0,7 мм.

Допущения и предложения на листе

Основа листа: взаимное расположение помещений, контур дома 9600 × 8000 и раскладка этажей подобраны проектировщиком под габариты помещений брифа; обмер и проект АР — задание (К-1); высота потолка 2900 мм — по брифу, не замерена; перекрытие 330 мм и отметка 2-го этажа +3,230 приняты; проект КР — задание (К-2); наружные стены 400 мм, перегородки 120 мм приняты (в брифе толщин нет) (К-1); разрешённая мощность 15 кВт принята по типовым ТУ для частного дома (К-4).

Знак «**» — предложение проектировщика, заказчиком не утверждено (согласовать с заказчиком): записи в реестре нет: Р7, Р8 — по образцу: Р7, Р8 и Р33 на высоте 1000 мм — верхний предел нормы (ПУЭ, п. 6.6.30, не выше 1 м); флаг решения снят; ЭВ4, КУП1 — по образцу: Добавлены выводы к вентиляторам: ЭВ4 (ВР1, ванная) и ЭВ5 (ВР3, санузел 2) — группа 3, высота 2389 мм, включение с основным светом, таймер выбега в вентиляторе; и коробки уравнивания потенциалов КУП1 (ванная) и КУП2 (санузел 2) — высота 300 мм, у входа, вне зон 0–2, проводник от шины РЕ щита ЩК, сече; ЭВ6 — по образцу: Добавлены электрические полотенцесушители IP44: П10 в ванной (480 мм, низ 900 мм) и П13 в санузле 2 (400 мм, низ 900 мм), выводы ЭВ6 и ЭВ7; мощность группы 13 — 2,4 кВт вместо 1,8 кВт.

См. лист открытых вопросов (лист 6, записи К-1, К-2, К-4).

1000 мм · печать 1:1

						ГД-2026-012-АИ
						Дом 120 м²
						Общая площадь 147,36* м² · * размеры приняты, не замерены (реестр — л. 6, К-1)
Изм.	Кол.уч	Лист	№ док.	Подп.	Дата	Дизайн-проект интерьера — Стадия: РП; Лист: 57; Листов: 130
Разраб.		Кырлан А.С.			19.10.26	**Раскладка плитки. Санузел второго этажа. Развёртки стен** — М 1:40
Пров.						**Кырлан Александр Сергеевич**
ГИП						
Н. контр.						
Утв.						

План полов · 1-й этаж

Покрытия, направление укладки, отметки чистого пола, стыки · размеры в мм · отметки в м

ПРЕДВАРИТЕЛЬНО · не для производства работ · открыто пунктов: 6 (реестр — л. 6)

Условные обозначения

- тип 1 — инженерная доска, линии — вдоль доски
- тип 2 — керамогранит 600×1200, сетка — формат плитки
- тип 3 — керамогранит 600×1200, сетка — формат плитки
- номер типа пола (экспликация полов)
- схема пола, без масштаба: плита — штриховка, стяжка — точки, звукоизоляция — зигзаг, гидроизоляция — утолщённая линия с заведением на стену
- направление укладки (длинная сторона доски)
- отметка чистого пола, м
- стык в проёме: решение не задано
- стык в проёме: порог
- СТ1 — марка стыка (ведомость стыков)
- стояк: К1 — канализация, В1 ХВС, Т3 — ГВС
- 1 — номер помещения, площадь м²

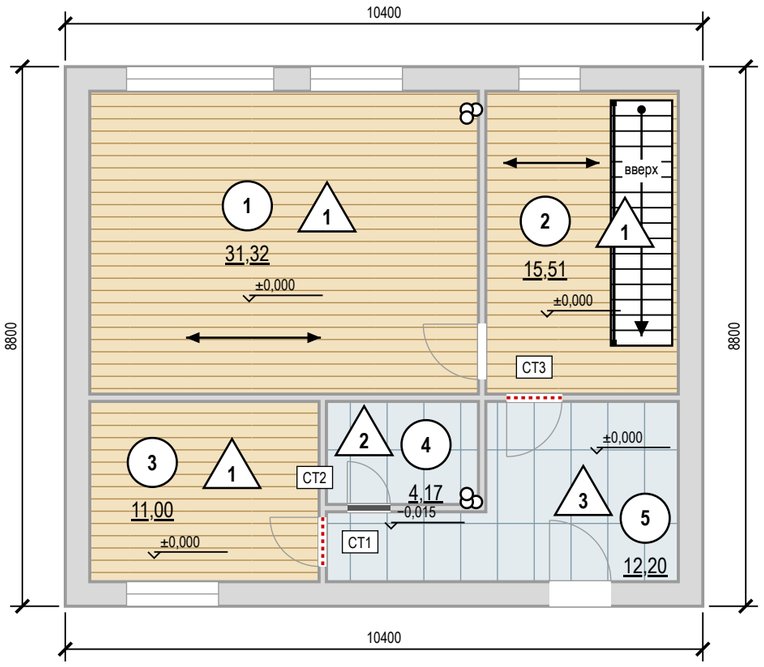

Экспликация полов

Номер помещения	Тип пола	Схема пола	Данные элементов пола (наименование, толщина, основание), мм	Площадь, м²
1, 2, 3	1		Инженерная доска на клею — 14 Стяжка ЦПС М200 — 50 Плита перекрытия Всего 64 мм; ЧП ±0,000, верх плиты −0,064	57,83
4	2		Керамогранит на клею С2 TE S1 — 14 Гидроизоляция обмазочная, 2 слоя, с заведением на стены 200 мм — 2 Стяжка ЦПС М200 — 33 Плита перекрытия Всего 49 мм; ЧП −0,015, верх плиты −0,064	4,17
5	3		Керамогранит на клею С2 TE S1 — 14 Стяжка ЦПС М200 — 50 Плита перекрытия Всего 64 мм; ЧП ±0,000, верх плиты −0,064	12,20
			Итого	**74,20**

Стыки покрытий в проёмах

Марка	Проём	Типы пола	Отметки ЧП	Решение
СТ1	3–5 (Д-2)	1 / 3	±0,000 / ±0,000	не задано
СТ2	4–5 (Д-3)	2 / 3	−0,015 / ±0,000	порог h=15 мм
СТ3	5–2 (Д-4)	3 / 1	±0,000 / ±0,000	не задано

Отметки по высоте

±0,000 чистый пол пом. 1–3, 5; отсчёт высот
−0,015 чистый пол пом. 4, ниже на 15 мм
−0,064* верх плиты — расчёт, не замер (задание на обмер)
сущ. пол снимается до плиты; не замерен (задание на обмер)

Допущения и предложения на листе

Основа листа: взаимное расположение помещений, контур дома 9600 × 8000 и раскладка этажей подобраны проектировщиком под габариты помещений брифа; обмер и проект АР — задание (К-1); высота потолка 2900 мм — по брифу, не замерена; перекрытие 330 мм и отметка 2-го этажа +3,230 приняты; проект КР — задание (К-2); наружные стены 400 мм, перегородки 120 мм приняты (в брифе толщин нет) (К-1); разрешённая мощность 15 кВт принята по типовым ТУ для частного дома (К-4).

Знак «**» — предложение проектировщика, заказчиком не утверждено (согласовать с заказчиком): записи в реестре нет: плинтус пом. 1–3, 5, фартук пом. 1 — артикул изделия не выбран: позиция описана характеристиками («аналог по характеристикам»), артикул выбирается при закупке.

См. лист открытых вопросов (лист 6, записи К-1, К-2, К-4).

Примечания

1. За отметку ±0,000 принят чистый пол, не существующий (блок отметок). Площади — по чистым размерам помещений, м²; размеры — в мм.
2. Стык разнотипных покрытий — по оси дверного полотна (под полотном в закрытом положении); решение стыка — по ведомости стыков.
3. Пол санузлов ниже смежных помещений на 15 мм за счёт меньшей толщины стяжки (верх плиты общий — по экспликации полов); гидроизоляция по стяжке с заведением на стены не менее 200 мм (СП 29.13330.2011, п. 7.2), до облицовки — тест проливом и акт скрытых работ.
4. Трубопроводы в конструкции пола не прокладываются: пирог пола 49–64 мм не вмещает выпуски канализации с уклоном — выпуски К1 ведутся по стенам над чистым полом в коробах.
5. Штучные покрытия (инженерная доска): направление — по стрелке; влажность основания по СМ не более 2,0 % (по ТУ изготовителя).
6. Ровность основания — просвет под 2-метровой рейкой не более 2 мм: пом. 1, 2, 3 (инженерная доска), пом. 4, 5 (керамогранит); проверить до укладки покрытия (СП 71.13330.2017, табл. 8.5).
7. Сетка на плитке — условная, в размер формата; точка старта и раскладка — по листу раскладки плитки.
8. Пироги полов — по экспликации полов: слои сверху вниз, толщины в мм; гидроизоляция мокрых зон — в пироге и в ведомости отделки; схема пола — без масштаба.

1000 мм · печать 1:1

Изм.	Кол.уч	Лист	№ док.	Подп.	Дата
Разраб.		Кырлан А.С.			19.10.26
Пров.					
ГИП					
Н. контр.					
Утв.					

ГД-2026-012-АИ

Дом 120 м²

Общая площадь 147,36* м² · * размеры приняты, не замерены (реестр — л. 6, К-1)

Дизайн-проект интерьера

Стадия	Лист	Листов
РП	58	130

План полов · 1-й этаж

М 1:100

Кырлан Александр Сергеевич

выпуск 19.10.2026 № 53e4f7ddae · стр. 62 из 160

План полов · 2-й этаж

Покрытия, направление укладки, отметки чистого пола, стыки · размеры в мм · отметки в м

ПРЕДВАРИТЕЛЬНО · не для производства работ · открыто пунктов: 6 (реестр — л. 6)

Отметки по высоте

±0,000	чистый пол пом. 6–12; отсчёт высот
−0,015	чистый пол пом. 13, ниже на 15 мм
−0,064*	верх плиты — расчёт, не замер (задание на обмер)
сущ. пол	снимается до плиты; не замерен (задание на обмер)

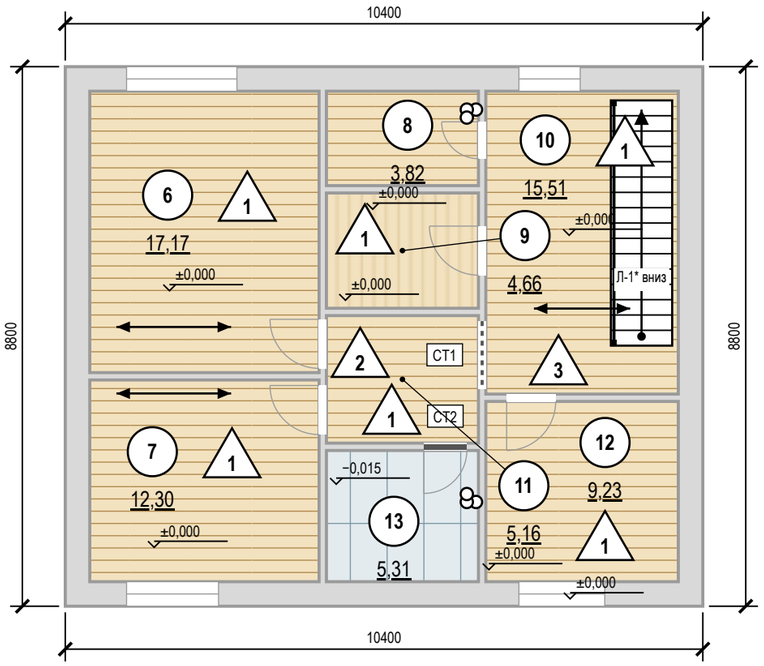

Экспликация полов

Номер помещения	Тип пола	Схема пола	Данные элементов пола (наименование, толщина, основание), мм	Площадь, м²
6, 7, 8, 10, 11, 12	1	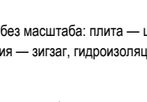	Инженерная доска на клею — 14 Стяжка ЦПС М200 — 50 Плита перекрытия Всего 64 мм; ЧП ±0,000, верх плиты −0,064	63,19
9	2		Инженерная доска, 1167-4250, 2100×127 мм, на клею ЧП ±0,000	4,66
13	3	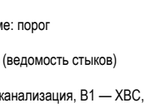	Керамогранит на клею С2 TE S1 — 14 Гидроизоляция обмазочная, 2 слоя, с заведением на стены 200 мм — 2 Стяжка ЦПС М200 — 33 Плита перекрытия Всего 49 мм; ЧП −0,015, верх плиты −0,064	5,31
			Итого	**73,16**

Стыки покрытий в проёмах

Марка	Проём	Типы пола	Отметки ЧП	Решение
СТ1	11–10 (Пр-1)	1 / 1	±0,000 / ±0,000	б/п
СТ2	13–11 (Д-8)	3 / 1	−0,015 / ±0,000	порог h=15 мм

Условные обозначения

- тип 1 — инженерная доска, линии — вдоль доски
- тип 2 — инженерная доска, линии — вдоль доски
- тип 3 — керамогранит 600×1200, сетка — формат плитки
- 1 — номер типа пола (экспликация полов)
- схема пола, без масштаба: плита — штриховка, стяжка — точки, звукоизоляция — зигзаг, гидроизоляция — утолщённая линия с заведением на стену
- направление укладки (длинная сторона доски)
- отметка чистого пола, м
- стык в проёме: без порога (б/п)
- стык в проёме: порог
- СТ1 — марка стыка (ведомость стыков)
- стояк: К1 — канализация, В1 — ХВС, Т3 — ГВС
- 1 — номер помещения, площадь м²

Допущения и предложения на листе

Основа листа: взаимное расположение помещений, контур дома 9600 × 8000 и раскладка этажей подобраны проектировщиком под габариты помещений брифа; обмер и проект АР — задание (К-1); высота потолка 2900 мм — по брифу, не замерена; перекрытие 330 мм и отметка 2-го этажа +3,230 приняты; проект КР — задание (К-2); наружные стены 400 мм, перегородки 120 мм приняты (в брифе толщин нет) (К-1); разрешённая мощность 15 кВт принята по типовым ТУ для частного дома (К-4).

Знак «*» — принято, не замерено и не подтверждено (замерить на объекте): К-3: Л-1 — место, тип и размеры лестницы брифом не заданы (только «лестница из холла 1-го этажа»): одномаршевая 17 × 190 × 250 вдоль стены Б холла — предложение проектировщика; конструкция и расчёт — проект КР.

Знак «**» — предложение проектировщика, заказчиком не утверждено (согласовать с заказчиком): записи в реестре нет: плинтус пом. 6, 8, 10, 11 — артикул изделия не выбран: позиция описана характеристиками («аналог по характеристикам»), артикул выбирается при закупке.

См. лист открытых вопросов (лист 6, записи К-1–К-4).

Примечания

1. За отметку ±0,000 принят чистый пол, не существующий (блок отметок). Площади — по чистым размерам помещений, м²; размеры — в мм.
2. Стык разнотипных покрытий — по оси дверного полотна (под полотном в закрытом положении); решение стыка — по ведомости стыков.
3. Пол санузлов ниже смежных помещений на 15 мм за счёт меньшей толщины стяжки (верх плиты общий — по экспликации полов); гидроизоляция по стяжке с заведением на стены не менее 200 мм (СП 29.13330.2011, п. 7.2), до облицовки — тест проливом и акт скрытых работ.
4. Трубопроводы в конструкции пола не прокладываются: пирог пола 49–64 мм не вмещает выпуски канализации с уклоном — выпуски К1 ведутся по стенам над чистым полом в коробах.
5. Штучные покрытия (инженерная доска): направление — по стрелке; влажность основания по СМ не более 2,0 % (по ТУ изготовителя).
6. Ровность основания — просвет под 2-метровой рейкой не более 2 мм: пом. 6, 7, 8, 9, 10, 11, 12 (инженерная доска), пом. 13 (керамогранит); проверить до укладки покрытия (СП 71.13330.2017, табл. 8.5).
7. Сетка на плитке — условная, в размер формата; точка старта и раскладка — по листу раскладки плитки.
8. Пироги полов — по экспликации полов: слои сверху вниз, толщины в мм; гидроизоляция мокрых зон — в пироге и в ведомости отделки; схема пола — без масштаба.

1000 мм · печать 1:1

Изм.	Кол.уч	Лист	№ док.	Подп.	Дата
Разраб.		Кырлан А.С.			19.10.26
Пров.					
ГИП					
Н. контр.					
Утв.					

ГД-2026-012-АИ

Дом 120 м²

Общая площадь 147,36* м² · * размеры приняты, не замерены (реестр — л. 6, К-1)

Дизайн-проект интерьера

Стадия	Лист	Листов
РП	59	130

План полов · 2-й этаж

М 1:100

Кырлан Александр Сергеевич

выпуск 19.10.2026 № 53e4f7ddae · стр. 63 из 160

Ведомость отделки помещений. Лист 1 из 2

Потолки, стены, низ стен, полы · площади в м², длины в м · отметки в м

Ведомость отделки помещений (форма 1 прил. А ГОСТ 21.501-2018). Лист 1 из 2

№	Наименование помещения	Потолок			Стены и перегородки			Низ стен (плинтус)			Пол		Примечание
		Вид отделки	Код цвета	S, м²	Вид отделки	Код цвета	S, м²	Вид отделки	Код цвета	L, м	Вид отделки	S, м²	
1	Гостиная-кухня 31,32 м²	Окраска, Tikkurila Anti-Reflex 2, глубокоматовая, 2 слоя, подготовка Q3	Little Greene No. 222	31,32	Окраска, Farrow & Ball Modern Emulsion, матовая, 2 слоя, подготовка Q3 Акцент — стена А: окраска, Farrow & Ball Modern Emulsion, матовая, 2 слоя, подготовка Q3 Фартук кухни (стена А, Б): облицовка керамогранитом, аналог: керамогранит под травертин, матовый, 1200×600×9 мм, клей C2 TE S1, затирка CG2WA	Tikkurila G503 NCS S 3050-R80B по артикулу	43,15 11,58 2,00	Плинтус МДФ h=80 мм, аналог: МДФ под покраску 80×16	Tikkurila G503	21,7	Инженерная доска, 1167-4250, 2100×127 мм, на клею; тип 1, отм. ЧП ±0,000	31,32	Н стен 2900 (до потолка); матовая моющаяся, класс 1 EN 13300 — осознанно вместо полуматовой; плинтус в цвет: стены
2	Холл с лестницей 15,51 м²	Окраска, Tikkurila Anti-Reflex 2, глубокоматовая, 2 слоя, подготовка Q3	Little Greene No. 222	15,51	Окраска, Farrow & Ball Modern Emulsion, матовая, 2 слоя, подготовка Q3	Tikkurila G503	34,65	Плинтус МДФ h=80 мм, аналог: МДФ под покраску 80×16	Tikkurila G503	11,1	Инженерная доска, 1167-4250, 2100×127 мм, на клею; тип 1, отм. ЧП ±0,000	15,51	Н стен 2900 (до потолка); матовая моющаяся, класс 1 EN 13300 — осознанно вместо полуматовой; плинтус в цвет: стены
3	Кабинет 11,00 м²	Окраска, Tikkurila Anti-Reflex 2, глубокоматовая, 2 слоя, подготовка Q3	Little Greene No. 222	11,00	Окраска, Farrow & Ball Modern Emulsion, матовая, 2 слоя, подготовка Q3 Акцент — стена А: окраска, Farrow & Ball Modern Emulsion, матовая, 2 слоя, подготовка Q3	Tikkurila G503 NCS S 5020-G90Y	23,97 10,85	Плинтус МДФ h=80 мм, аналог: МДФ под покраску 80×16	Tikkurila G503	12,6	Инженерная доска, 1167-4250, 2100×127 мм, на клею; тип 1, отм. ЧП ±0,000	11,00	Н стен 2900 (до потолка); плинтус в цвет: стены
4	Санузел гостевой 4,17 м²	Окраска, Tikkurila Luja 7, матовая, 2 слоя, подготовка Q3	Little Greene No. 222	4,17	Облицовка плиткой, A8UZ, 600×1200×9 мм, клей C2 TE S1, затирка CG2WA	Atlas Concorde A8UZ	17,40	нет			Керамогранит, A8UZ, 600×1200×9 мм; тип 2, отм. ЧП −0,015	4,17	Н стен 2915 (до потолка); гидроизоляция обмазочная, 2 слоя, с заведением на стены 200 мм (по пирогу пола); тест проливом и акт скрытых работ
5	Прихожая 12,20 м²	Окраска, Tikkurila Anti-Reflex 2, глубокоматовая, 2 слоя, подготовка Q3	Little Greene No. 222	12,20	Окраска, Farrow & Ball Modern Emulsion, матовая, 2 слоя, подготовка Q3	Tikkurila G503	43,20	Плинтус МДФ h=80 мм, аналог: МДФ под покраску 80×16	Tikkurila G503	14,0	Керамогранит, A8UZ, 600×1200×9 мм; тип 3, отм. ЧП ±0,000	12,20	Н стен 2900 (до потолка); матовая моющаяся, класс 1 EN 13300 — осознанно вместо полуматовой; плинтус в цвет: стены
6	Спальня родителей 17,17 м²	Окраска, Tikkurila Anti-Reflex 2, глубокоматовая, 2 слоя, подготовка Q3	Little Greene No. 222	17,17	Окраска, Farrow & Ball Modern Emulsion, матовая, 2 слоя, подготовка Q3 Акцент — стена А: окраска, Farrow & Ball Modern Emulsion, матовая, 2 слоя, подготовка Q3	Tikkurila G503 Farrow & Ball No. 89	35,79 8,15	Плинтус МДФ h=80 мм, аналог: МДФ под покраску 80×16	Tikkurila G503	15,9	Инженерная доска, 1167-4250, 2100×127 мм, на клею; тип 1, отм. ЧП ±0,000	17,17	Н стен 2900 (до потолка); плинтус в цвет: стены
7	Детская 12,30 м²	Окраска, Tikkurila Anti-Reflex 2, глубокоматовая, 2 слоя, подготовка Q3	Little Greene No. 222	12,30	Окраска, Farrow & Ball Modern Emulsion, матовая, 2 слоя, подготовка Q3 Акцент — стена А: окраска, Farrow & Ball Modern Emulsion, матовая, 2 слоя, подготовка Q3	Tikkurila G503 Farrow & Ball No. 66	26,07 10,85	Плинтус МДФ h=69 мм, SX165	Tikkurila G503	13,3	Инженерная доска, 1167-4250, 2100×127 мм, на клею; тип 1, отм. ЧП ±0,000	12,30	Н стен 2900 (до потолка); плинтус в цвет: стены
8	Гардеробная 3,82 м²	Окраска, Tikkurila Anti-Reflex 2, глубокоматовая, 2 слоя, подготовка Q3	Little Greene No. 222	3,82	Окраска, Tikkurila Harmony, матовая, 2 слоя, подготовка Q3	Little Greene No. 222	22,06	Плинтус МДФ h=80 мм, аналог: МДФ под покраску 80×16	Little Greene No. 222	7,4	Инженерная доска, 1167-4250, 2100×127 мм, на клею; тип 1, отм. ЧП ±0,000	3,82	Н стен 2900 (до потолка); плинтус в цвет: стены

Примечания

1. Ведомость продолжена на листе 2 из 2; итоги, сводка площадей и примечания — на последнем листе ведомости.

Допущения и предложения на листе

Основа листа: взаимное расположение помещений, контур дома 9600 × 8000 и раскладка этажей подобраны проектировщиком под габариты помещений брифа; обмер и проект АР — задание (К-1); высота потолка 2900 мм — по брифу, не замерена; перекрытие 330 мм и отметка 2-го этажа +3,230 приняты; проект КР — задание (К-2); наружные стены 400 мм, перегородки 120 мм приняты (в брифе толщин нет) (К-1); разрешённая мощность 15 кВт принята по типовым ТУ для частного дома (К-4).

Знак «**» — предложение проектировщика, заказчиком не утверждено (согласовать с заказчиком): записи в реестре нет: плинтус пом. 1–3, 5, 6, 8, 10, 11, фартук пом. 1 — артикул изделия не выбран: позиция описана характеристиками («аналог по характеристикам»), артикул выбирается при закупке.

См. лист открытых вопросов (лист 6, записи К-1, К-2, К-4).

Изм.	Кол.уч	Лист	№ док.	Подп.	Дата
Разраб.		Кырлан А.С.			19.10.26
Пров.					
ГИП					
Н. контр.					
Утв.					

ГД-2026-012-АИ

Дом 120 м²

Общая площадь 147,36* м² · * размеры приняты, не замерены (реестр — л. 6, К-1)

Дизайн-проект интерьера

Стадия	Лист	Листов
РП	60	130

Ведомость отделки помещений. Лист 1 из 2

М б/м

Кырлан Александр Сергеевич

выпуск 19.10.2026 № 53e4f7ddae · стр. 64 из 160

Ведомость отделки помещений. Лист 2 из 2

Потолки, стены, низ стен, полы · площади в м², длины в м · отметки в м

Ведомость отделки помещений (форма 1 прил. А ГОСТ 21.501-2018). Лист 2 из 2

№	Наименование помещения	Потолок			Стены и перегородки			Низ стен (плинтус)			Пол		Примечание
		Вид отделки	Код цвета	S, м²	Вид отделки	Код цвета	S, м²	Вид отделки	Код цвета	L, м	Вид отделки	S, м²	
9	Кладовая 4,66 м²	Окраска, Tikkurila, глубокоматовая	NCS S 0300-N	4,66	Окраска, Tikkurila, матовая, подготовка Q3	NCS S 0502-Y	23,61	Плинтус МДФ h=69 мм, SX165	NCS S 0300-N	7,9	Инженерная доска, 1167-4250, 2100×127 мм, на клею; тип 4, отм. ЧП ±0,000	4,66	Н стен 2900 (до потолка)
10	Холл второго этажа 15,51 м²	Окраска, Tikkurila Anti-Reflex 2, глубокоматовая, 2 слоя, подготовка Q3	Little Greene No. 222	15,51	Окраска, Farrow & Ball Modern Emulsion, матовая, 2 слоя, подготовка Q3	Tikkurila G503	34,65	Плинтус МДФ h=80 мм, аналог: МДФ под покраску 80×16	Tikkurila G503	11,1	Инженерная доска, 1167-4250, 2100×127 мм, на клею; тип 1, отм. ЧП ±0,000	15,51	Н стен 2900 (до потолка); матовая моющаяся, класс 1 EN 13300 — осознанно вместо полуматовой; плинтус в цвет: стены
11	Коридор второго этажа 5,16 м²	Окраска, Tikkurila Anti-Reflex 2, глубокоматовая, 2 слоя, подготовка Q3	Little Greene No. 222	5,16	Окраска, Farrow & Ball Modern Emulsion, матовая, 2 слоя, подготовка Q3	Tikkurila G503	19,31	Плинтус МДФ h=80 мм, аналог: МДФ под покраску 80×16	Tikkurila G503	5,7	Инженерная доска, 1167-4250, 2100×127 мм, на клею; тип 1, отм. ЧП ±0,000	5,16	Н стен 2900 (до потолка); матовая моющаяся, класс 1 EN 13300 — осознанно вместо полуматовой; плинтус в цвет: стены
12	Детская вторая 9,23 м²	Окраска, Tikkurila Anti-Reflex 2, глубокоматовая, 2 слоя, подготовка Q3	Little Greene No. 222	9,23	Окраска, Farrow & Ball Modern Emulsion, матовая, 2 слоя, подготовка Q3 Акцент — стена А: окраска, Farrow & Ball Modern Emulsion, матовая, 2 слоя, подготовка Q3	Tikkurila G503 Tikkurila H440	24,13 7,43	Плинтус МДФ h=69 мм, SX165	Tikkurila G503	11,4	Инженерная доска, 1167-4250, 2100×127 мм, на клею; тип 1, отм. ЧП ±0,000	9,23	Н стен 2900 (до потолка); плинтус в цвет: стены
13	Санузел второго этажа 5,31 м²	Окраска, Tikkurila Luja 7, матовая, 2 слоя, подготовка Q3	Little Greene No. 222	5,31	Облицовка плиткой, A8UZ, 600×1200×9 мм, клей C2 TE S1, затирка CG2WA	Atlas Concorde A8UZ	19,06	нет			Керамогранит, A8UZ, 600×1200×9 мм; тип 2, отм. ЧП −0,015	5,31	Н стен 2915 (до потолка); гидроизоляция обмазочная, 2 слоя, с заведением на стены 200 мм (по пирогу пола); тест проливом и акт скрытых работ
	Итого			**147,36**			**417,89**			**131,9**		**147,36**	

Примечания

1. Площади поверхностей — по чистым граням стен до отделки: стены = периметр × высоту от чистого пола помещения до низа потолка минус проёмы (облицовка плиткой — до верха облицовки); плинтус = периметр минус дверные проёмы; пол и потолок — по площади помещения. Количество плиток по раскладке. Площади помещений — с учётом всех частей помещения; откосы в площадь стен не входят.
2. Акцентные стены и фартук — отдельными строками, их площадь вычтена из основной отделки стен помещения; фартук — над нижними модулями кухни от столешницы до низа навесных шкафов, где шкафов нет — на 600 мм.
3. Плинтус — длина по периметру за вычетом дверных проёмов; примыкания к наличникам и встроенной мебели — по развёрткам.
4. Формат плитки — Ш×В×Т (ширина × высота в положении укладки × толщина), мм; на полу — вдоль стен А/В × вдоль стен Б/Г.
5. Коды цвета — по веерам производителей; колеровка каждой краски одной партией, проверка выкраса при свете D65 и при лампах проекта.
6. Уровни подготовки Q1–Q4 — система Knauf, не норма ГОСТ/СП; допуски поверхностей — по СП 71.13330.2017 (действующая редакция).
7. «аналог:» — изделие задано характеристиками, марку и артикул согласовать с заказчиком до закупки.
8. Сводка площадей по материалам, м²: потолок — Little Greene No. 222 Anti-Reflex 2 — 133,22; потолок — Little Greene No. 222 Luja 7 — 9,48; потолок — NCS S 0300-N — 4,66; стены — Tikkurila G503 Modern Emulsion — 284,92; стены — NCS S 3050-R80B Modern Emulsion — 11,58; стены — NCS S 5020-G90Y Modern Emulsion — 10,85; стены — облицовка плиткой 600×1200×9 мм, Atlas Concorde A8UZ — 36,46; стены — Farrow & Ball No. 89 Modern Emulsion — 8,15; стены — Farrow & Ball No. 66 Modern Emulsion — 10,85; стены — Little Greene No. 222 Harmony — 22,06; стены — NCS S 0502-Y 23,61; стены — Tikkurila H440 Modern Emulsion — 7,43; фартук — облицовка керамогранитом 1200×600×9 мм — 2,00.

Допущения и предложения на листе

Основа листа: взаимное расположение помещений, контур дома 9600 × 8000 и раскладка этажей подобраны проектировщиком под габариты помещений брифа; обмер и проект АР — задание (К-1); высота потолка 2900 мм — по брифу, не замерена; перекрытие 330 мм и отметка 2-го этажа +3,230 приняты; проект КР — задание (К-2); наружные стены 400 мм, перегородки 120 мм приняты (в брифе толщин нет) (К-1); разрешённая мощность 15 кВт принята по типовым ТУ для частного дома (К-4).

Знак «**» — предложение проектировщика, заказчиком не утверждено (согласовать с заказчиком): записи в реестре нет: плинтус пом. 1–3, 5, 6, 8, 10, 11, фартук пом. 1 — артикул изделия не выбран: позиция описана характеристиками («аналог по характеристикам»), артикул выбирается при закупке.

См. лист открытых вопросов (лист 6, записи К-1, К-2, К-4).

Изм.	Кол.уч	Лист	№ док.	Подп.	Дата
Разраб.		Кырлан А.С.			19.10.26
Пров.					
ГИП					
Н. контр.					
Утв.					

ГД-2026-012-АИ

Дом 120 м²

Общая площадь 147,36* м² · * размеры приняты, не замерены (реестр — л. 6, К-1)

Дизайн-проект интерьера	Стадия	Лист	Листов
	РП	61	130
Ведомость отделки помещений. Лист 2 из 2 М б/м	**Кырлан Александр Сергеевич**		

Колерная карта · 1-й этаж

Цвета и материалы по помещениям · палитра проекта · выкрасы на согласование

ПРЕДВАРИТЕЛЬНО · не для производства работ · открыто пунктов: 6 (реестр — л. 6)

Колерная карта по помещениям

Помещение	Поверхность	Образец	Поз.	Система и код цвета	Производитель, линейка / материал, артикул	Блеск	Класс EN 13300	LRV	Площадь
1. Гостиная-кухня 31,32 м²	стены		**K1**	Tikkurila G503	Farrow & Ball · Modern Emulsion	матовая	1	89	43,1 м²
	акцент А		**K2**	NCS S 3050-R80B	Farrow & Ball · Modern Emulsion	матовая	1	≈13	11,6 м²
	потолок		**K3**	Little Greene No. 222	Tikkurila · Anti-Reflex 2	глубокомат.	2	92	31,3 м²
	пол		**KM1**	по образцу	Coswick · Вековые традиции				31,3 м²
	плинтус		**K4**	Tikkurila G503	МДФ · в цвет Tikkurila			89	21,7 м
	фартук		**KM2**	по образцу	керамогранит · аналог по хар.				2,0 м²
2. Холл с лестницей 15,51 м²	стены		**K1**	Tikkurila G503	Farrow & Ball · Modern Emulsion	матовая	1	89	41,6 м²
	потолок		**K3**	Little Greene No. 222	Tikkurila · Anti-Reflex 2	глубокомат.	2	92	15,5 м²
	пол		**KM1**	по образцу	Coswick · Вековые традиции				15,5 м²
	плинтус		**K4**	Tikkurila G503	МДФ · в цвет Tikkurila			89	14,4 м
3. Кабинет 11 м²	стены		**K1**	Tikkurila G503	Farrow & Ball · Modern Emulsion	матовая	1	89	24,0 м²
	акцент А		**K5**	NCS S 5020-G90Y	Farrow & Ball · Modern Emulsion	матовая	1	≈20	10,8 м²
	потолок		**K3**	Little Greene No. 222	Tikkurila · Anti-Reflex 2	глубокомат.	2	92	11,0 м²
	пол		**KM1**	по образцу	Coswick · Вековые традиции				11,0 м²
	плинтус		**K4**	Tikkurila G503	МДФ · в цвет Tikkurila			89	12,6 м
4. Санузел гостевой 4,17 м²	стены		**K6**	Atlas Concorde A8UZ	Atlas Concorde · Marvel Travertine				18,5 м²
	потолок		**K7**	Little Greene No. 222	Tikkurila · Luja 7	матовая	1	92	4,2 м²
	пол		**K6**	Atlas Concorde A8UZ	Atlas Concorde · Marvel Travertine				4,2 м²
5. Прихожая 12,2 м²	стены		**K1**	Tikkurila G503	Farrow & Ball · Modern Emulsion	матовая	1	89	43,2 м²
	потолок		**K3**	Little Greene No. 222	Tikkurila · Anti-Reflex 2	глубокомат.	2	92	12,2 м²
	пол		**K6**	Atlas Concorde A8UZ	Atlas Concorde · Marvel Travertine				12,2 м²
	плинтус		**K4**	Tikkurila G503	МДФ · в цвет Tikkurila			89	14,0 м

Перечень выкрасов на согласование

№	Код	Бренд / веер	Пом. / стена	Подложка	Формат	Статус
1	G503	Tikkurila	1, 2, 3, 5	ГКЛ, загрунтованный под эту краску; МДФ, загрунтованный под эмаль	600×1000; 300×600	к выполнению
2	S 3050-R80B	NCS Farrow & Ball	1 A	ГКЛ, загрунтованный под эту краску	600×1000	к выполнению
3	No. 222	Little Greene	1, 2, 3, 4, 5	ГКЛ, загрунтованный под эту краску	600×1000	к выполнению
4	S 5020-G90Y	NCS Farrow & Ball	3 A	ГКЛ, загрунтованный под эту краску	600×1000	к выполнению

Допущения и предложения на листе

Основа листа: взаимное расположение помещений, контур дома 9600 × 8000 и раскладка этажей подобраны проектировщиком под габариты помещений брифа; обмер и проект АР — задание (К-1); высота потолка 2900 мм — по брифу, не замерена; перекрытие 330 мм и отметка 2-го этажа +3,230 приняты; проект КР — задание (К-2); наружные стены 400 мм, перегородки 120 мм приняты (в брифе толщин нет) (К-1); разрешённая мощность 15 кВт принята по типовым ТУ для частного дома (К-4).

Знак «**» — предложение проектировщика, заказчиком не утверждено (согласовать с заказчиком): записи в реестре нет: плинтус пом. 1–3, 5, 6, 8, 10, 11, фартук пом. 1 — артикул изделия не выбран: позиция описана характеристиками («аналог по характеристикам»), артикул выбирается при закупке.

См. лист открытых вопросов (лист 6, записи К-1, К-2, К-4).

Примечания

1. Цвет утверждается только по выкрасу на объекте: формат от А3 до 1000×1000 мм на загрунтованном ГКЛ, в 2 слоя (как на стене), не на белой шпаклёвке; смотреть днём и при свете проекта своего помещения, рядом с образцами пола и фасадов. Подпись на обороте: код, бренд и веер, дата.
2. Колеровка машинная в колеровочном центре бренда; каждый код — за один проход, одной партией на весь объём. Колеровщику передаётся только система и код утверждённого веера; плашки и HEX на листе — ориентир, печать не является эталоном цвета.
3. Класс мокрого истирания — EN 13300 (ISO 11998); блеск — по ГОСТ 31975 (ISO 2813), геометрия 60°. LRV — пересчёт координаты L* каталога производителя (Y = ((L*+16)/116)³); «≈» — расчёт по HEX, справочно.
4. Площади поверхностей — тем же способом и с теми же цифрами, что в ведомости отделки (способ счёта — в общих указаниях); объём краски к заказу, фасовка и материалы КМ — в спецификации отделочных материалов.
5. Перечень выкрасов составлен по кодам колерной карты; к основному тону стен добавить на выкрас 2 соседних тона того же веера (светлее и темнее), статус отмечать в графе «Статус» при согласовании.

Схема квартиры: цвет стен и акценты (б/м)

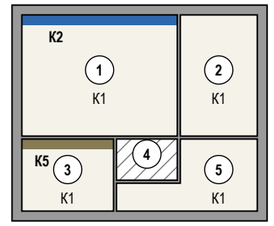

Схема палитры проекта

Стиль: Средиземноморский 60% + Скандинавский 40% · схема: complement

основной	основной	основной	второстепенный	второстепенный	второстепенный	акцентный	акцентный	акцентный
Tikkurila G503	Farrow & Ball No. 239	Little Greene No. 222	NCS S 1010-Y20R	Farrow & Ball No. 89	Farrow & Ball No. 292	NCS S 3050-R80B	Farrow & Ball No. 66	NCS S 5020-G90Y
Calla LRV 89 стены 1,2,3,5; плинтус 1,2,3,5	Wimborne White – белый с каплей тёплой охры LRV ≈89 в отделке не применён	Loft White LRV 92 потолок 1,2,3,4,5; текстиль/декор 1,3	Светлый песок / известняк LRV 75 текстиль/декор 1,3	Lulworth Blue – светлая морская лазурь LRV ≈45 в отделке не применён	Treron – серо-оливковая листва LRV 15 в отделке не применён	Эгейский синий LRV ≈13 акцент 1; текстиль/декор 1	India Yellow – охра / горчица итальянских фасадов LRV 36 в отделке не применён	Олива LRV ≈20 акцент 3; текстиль/декор 3

План 60/30/10

60%	30%	10%

Окраска, факт — по площади стен, акцентов, потолков

85%	8%	7%

окрашено всего 267,1 м²; второстепенный тон несут мебель и текстиль

Текстиль и декор в цветах вне палитры проекта

Tikkurila X463 X463 Sandstone — песчаник — пом. 1 (T15, T16, T19), 3 (T9)

Условные обозначения

- **K1** Tikkurila G503 · Calla · Modern Emulsion · матовая · кл. 1
- **K2** NCS S 3050-R80B · Эгейский синий · Farrow & Ball Modern Emulsion · матовая · кл. 1
- **K3** Little Greene No. 222 · Loft White · Anti-Reflex 2 · глубокомат. · кл. 2
- **K4** Tikkurila G503 · Calla · МДФ
- **K5** NCS S 5020-G90Y · Олива · Farrow & Ball Modern Emulsion · матовая · кл. 1
- **K6** Atlas Concorde A8UZ · Marvel Travertine · Marvel Travertine
- **K7** Little Greene No. 222 · Loft White · Luja 7 · матовая · кл. 1
- **KM1** инженерная доска · 1167-4250
- **KM2** аналог: керамогранит под травертин, матовый, 1200×600×9 мм

дерево (доска, паркет, ламинат) — рисунок досок

керамогранит, плитка, камень — сетка швов по формату

HEX не задан — цвет только по коду и вееру

К — позиция окраски (код + продукт + блеск), КМ — позиция материала, тон КМ — по описанию артикула, эталон — образец материала; ≈ LRV — расчёт по HEX, справочно

Изм.	Кол.уч	Лист	№ док.	Подп.	Дата
Разраб.		Кырлан А.С.			19.10.26
Пров.					
ГИП					
Н. контр.					
Утв.					

ГД-2026-012-АИ

Дом 120 м²

Общая площадь 147,36* м² · * размеры приняты, не замерены (реестр — л. 6, К-1)

Дизайн-проект интерьера

Стадия	Лист	Листов
РП	62	130

Колерная карта · 1-й этаж

М б/м

Кырлан Александр Сергеевич

выпуск 19.10.2026 № 53e4f7ddae · стр. 66 из 160

Колерная карта · 2-й этаж

Цвета и материалы по помещениям · палитра проекта · выкрасы на согласование

Колерная карта по помещениям

Помещение	Поверхность	Образец	Поз.	Система и код цвета	Производитель, линейка / материал, артикул	Блеск	Класс EN 13300	LRV	Площадь
6. Спальня родителей 17,17 м²	стены		**K1**	Tikkurila G503	Farrow & Ball · Modern Emulsion	матовая	1	89	35,8 м²
	акцент А		**K2**	Farrow & Ball No. 89	Farrow & Ball · Modern Emulsion	матовая	1	≈45	8,1 м²
	потолок		**K3**	Little Greene No. 222	Tikkurila · Anti-Reflex 2	глубокомат.	2	92	17,2 м²
	пол		**KM1**	по образцу	Coswick · Вековые традиции				17,2 м²
	плинтус		**K4**	Tikkurila G503	МДФ · в цвет Tikkurila			89	15,9 м
7. Детская 12,3 м²	стены		**K1**	Tikkurila G503	Farrow & Ball · Modern Emulsion	матовая	1	89	26,1 м²
	акцент А		**K5**	Farrow & Ball No. 66	Farrow & Ball · Modern Emulsion	матовая	1	36	10,8 м²
	потолок		**K3**	Little Greene No. 222	Tikkurila · Anti-Reflex 2	глубокомат.	2	92	12,3 м²
	пол		**KM1**	по образцу	Coswick · Вековые традиции				12,3 м²
	плинтус		**K6**	Tikkurila G503	Orac Decor · Contour (Luxxus)			89	13,3 м
8. Гардеробная 3,82 м²	стены		**K7**	Little Greene No. 222	Tikkurila · Harmony	матовая	1	92	22,1 м²
	потолок		**K3**	Little Greene No. 222	Tikkurila · Anti-Reflex 2	глубокомат.	2	92	3,8 м²
	пол		**KM1**	по образцу	Coswick · Вековые традиции				3,8 м²
	плинтус		**K8**	Little Greene No. 222	МДФ · в цвет Little Greene			92	7,4 м
9. Кладовая 4,66 м²	стены		**K9**	NCS S 0502-Y	Tikkurila	матовая	2	86	23,6 м²
	потолок		**K10**	NCS S 0300-N	Tikkurila	глубокомат.	2	92	4,7 м²
	пол		**KM1**	по образцу	Coswick · Вековые традиции				4,7 м²
	плинтус		**K11**	NCS S 0300-N	Orac Decor · Contour (Luxxus)	полуматов.		92	7,9 м
10. Холл второго этажа 15,51 м²	стены		**K1**	Tikkurila G503	Farrow & Ball · Modern Emulsion	матовая	1	89	38,4 м²
	потолок		**K3**	Little Greene No. 222	Tikkurila · Anti-Reflex 2	глубокомат.	2	92	15,5 м²
	пол		**KM1**	по образцу	Coswick · Вековые традиции				15,5 м²
	плинтус		**K4**	Tikkurila G503	МДФ · в цвет Tikkurila			89	12,9 м
11. Коридор второго этажа 5,16 м²	стены		**K1**	Tikkurila G503	Farrow & Ball · Modern Emulsion	матовая	1	89	19,3 м²
	потолок		**K3**	Little Greene No. 222	Tikkurila · Anti-Reflex 2	глубокомат.	2	92	5,2 м²
	пол		**KM1**	по образцу	Coswick · Вековые традиции				5,2 м²
	плинтус		**K4**	Tikkurila G503	МДФ · в цвет Tikkurila			89	5,7 м
12. Детская вторая 9,23 м²	стены		**K1**	Tikkurila G503	Farrow & Ball · Modern Emulsion	матовая	1	89	24,1 м²
	акцент А		**K12**	Tikkurila H440	Farrow & Ball · Modern Emulsion	матовая	1	≈51	7,4 м²
	потолок		**K3**	Little Greene No. 222	Tikkurila · Anti-Reflex 2	глубокомат.	2	92	9,2 м²
	пол		**KM1**	по образцу	Coswick · Вековые традиции				9,2 м²
	плинтус		**K6**	Tikkurila G503	Orac Decor · Contour (Luxxus)			89	11,4 м
13. Санузел второго этажа 5,31 м²	стены		**K13**	Atlas Concorde A8UZ	Atlas Concorde · Marvel Travertine				20,7 м²
	потолок		**K14**	Little Greene No. 222	Tikkurila · Luja 7	матовая	1	92	5,3 м²
	пол		**K13**	Atlas Concorde A8UZ	Atlas Concorde · Marvel Travertine				5,3 м²

Схема палитры проекта

Стиль: Средиземноморский 60% + Скандинавский 40% · схема: complement

основной	основной	основной	второстепенный	второстепенный	второстепенный	акцентный	акцентный	акцентный
Tikkurila G503	Farrow & Ball No. 239	Little Greene No. 222	NCS S 1010-Y20R	Farrow & Ball No. 89	Farrow & Ball No. 292	NCS S 3050-R80B	Farrow & Ball No. 66	NCS S 5020-G90Y
Calla LRV 89 стены 6,7,10,11,12; плинтус 6,7,10,11,12	Wimborne White – белый с каплей тёплой охры LRV ≈89 в отделке не применён	Loft White LRV 92 потолок 6,7,8,10,11,12,13; стены 8; плинтус 8; текстиль/декор 6,7,12	Светлый песок / известняк LRV 75 текстиль/декор 6,7,12	Lulworth Blue – светлая морская лазурь LRV ≈45 акцент 6; текстиль/декор 6	Treron – серо-оливковая листва LRV 15 в отделке не применён	Эгейский синий LRV ≈13 в отделке не применён	India Yellow – охра / горчица итальянских фасадов LRV 36 акцент 7; текстиль/декор 7	Олива LRV ≈20 в отделке не применён

План 60/30/10

Окраска, факт — по площади стен, акцентов, потолков

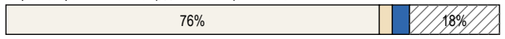

окрашено всего 309,7 м²; второстепенный тон несут мебель и текстиль

Текстиль и декор в цветах вне палитры проекта

- Tikkurila X395 X395 Playa — влажный пляжный песок — пом. 6 (T3)
- Tikkurila X463 X463 Sandstone — песчаник — пом. 7 (T22), 12 (T28)

Условные обозначения

- **K1** Tikkurila G503 · Calla · Modern Emulsion · матовая · кл. 1
- **K2** Farrow & Ball No. 89 · Lulworth Blue — светлая морская лазурь · Modern Emulsion · матовая · кл. 1
- **K3** Little Greene No. 222 · Loft White · Anti-Reflex 2 · глубокомат. · кл. 2
- **K4** Tikkurila G503 · Calla · МДФ
- **K5** Farrow & Ball No. 66 · India Yellow — охра / горчица итальянских фасадов · Modern Emulsion · матовая · кл. 1
- **K6** Tikkurila G503 · Calla · Contour (Luxxus)
- **K7** Little Greene No. 222 · Loft White · Harmony · матовая · кл. 1
- **K8** Little Greene No. 222 · Loft White · МДФ
- дерево (доска, паркет, ламинат) — рисунок досок
- HEX не задан — цвет только по коду и вееру
- **K9** NCS S 0502-Y · Tikkurila · матовая · кл. 2
- **K10** NCS S 0300-N · Tikkurila · глубокомат. · кл. 2
- **K11** NCS S 0300-N · Orac Decor Contour (Luxxus) · полуматов.
- **K12** Tikkurila H440 · H440 Wave — бирюзово-голубая вода · Modern Emulsion · матовая · кл. 1
- **K13** Atlas Concorde A8UZ · Marvel Travertine · Marvel Travertine
- **K14** Little Greene No. 222 · Loft White · Luja 7 · матовая · кл. 1
- **KM1** инженерная доска · 1167-4250

K — позиция окраски (код + продукт + блеск), KM — позиция материала, тон KM — по описанию артикула, эталон — образец материала; ≈ LRV — расчёт по HEX, справочно

Перечень выкрасов на согласование

№	Код	Бренд / веер	Пом. / стена	Подложка	Формат	Статус
1	G503	Tikkurila	6, 7, 10, 11, 12	ГКЛ, загрунтованный под эту краску; МДФ, загрунтованный под эмаль	600×1000; 300×600	к выполнению
2	No. 89	Farrow & Ball	6 A	ГКЛ, загрунтованный под эту краску	600×1000	к выполнению
3	No. 222	Little Greene	6, 7, 8, 10, 11, 12, 13	ГКЛ, загрунтованный под эту краску; МДФ, загрунтованный под эмаль	600×1000; 300×600	к выполнению

… ещё 4 выкрасов — в ведомости отделки

Примечания

1. Цвет утверждается только по выкрасу на объекте: формат от А3 до 1000×1000 мм на загрунтованном ГКЛ, в 2 слоя (как на стене), не на белой шпаклёвке; смотреть днём и при свете проекта своего помещения, рядом с образцами пола и фасадов. Подпись на обороте: код, бренд и веер, дата.
2. Колеровка машинная в колеровочном центре бренда; каждый код — за один проход, одной партией на весь объём. Колеровщику передаётся только система и код утверждённого веера; плашки и HEX на листе — ориентир, печать не является эталоном цвета.
3. Класс мокрого истирания — EN 13300 (ISO 11998); блеск — по ГОСТ 31975 (ISO 2813), геометрия 60°. LRV — пересчёт координаты L* каталога производителя (Y = ((L*+16)/116)³); «≈» — расчёт по HEX, справочно.
4. Площади поверхностей — тем же способом и с теми же цифрами, что в ведомости отделки (способ счёта — в общих указаниях); объём краски к заказу, фасовка и материалы КМ — в спецификации отделочных материалов.
5. Перечень выкрасов составлен по кодам колерной карты; к основному тону стен добавить на выкрас 2 соседних тона того же веера (светлее и темнее), статус отмечать в графе «Статус» при согласовании.

Допущения и предложения на листе. Знак «**» предложено (согласовать): плинтус пом. 1–3, 5, 6, 8, 10, 11, фартук пом. 1. См. лист открытых вопросов (лист 6).

Изм.	Кол.уч	Лист	№ док.	Подп.	Дата
Разраб.		Кырлан А.С.			19.10.26
Пров.					
ГИП					
Н. контр.					
Утв.					

ГД-2026-012-АИ

Дом 120 м²

Общая площадь 147,36* м² · * размеры приняты, не замерены (реестр — л. 6, К-1)

Дизайн-проект интерьера

Стадия	Лист	Листов
РП	63	130

Колерная карта · 2-й этаж

М б/м

Кырлан Александр Сергеевич

Колерная карта

Цвета и материалы по помещениям · выкрасы на согласование · лист 2 из 2

Колерная карта по помещениям (продолжение)

Помещение	Поверхность	Образец	Поз.	Система и код цвета	Производитель, линейка / материал, артикул	Блеск	Класс EN 13300	LRV	Площадь
7. Детская 12,3 м²	стены		**K1**	Tikkurila G503	Farrow & Ball · Modern Emulsion	матовая	1	89	26,1 м²
	акцент А		**K9**	Farrow & Ball No. 66	Farrow & Ball · Modern Emulsion	матовая	1	36	10,8 м²
	потолок		**K3**	Little Greene No. 222	Tikkurila · Anti-Reflex 2	глубокомат.	2	92	12,3 м²
	пол		**KM1**	по образцу	Coswick · Вековые традиции				12,3 м²
	плинтус		**K10**	Tikkurila G503	Orac Decor · Contour (Luxxus)			89	13,3 м
8. Гардеробная 3,82 м²	стены		**K11**	Little Greene No. 222	Tikkurila · Harmony	матовая	1	92	22,1 м²
	потолок		**K3**	Little Greene No. 222	Tikkurila · Anti-Reflex 2	глубокомат.	2	92	3,8 м²
	пол		**KM1**	по образцу	Coswick · Вековые традиции				3,8 м²
	плинтус		**K12**	Little Greene No. 222	МДФ · в цвет Little Greene			92	7,4 м
9. Кладовая 4,66 м²	стены		**K13**	NCS S 0502-Y	Tikkurila	матовая	2	86	23,6 м²
	потолок		**K14**	NCS S 0300-N	Tikkurila	глубокомат.	2	92	4,7 м²
	пол		**KM1**	по образцу	Coswick · Вековые традиции				4,7 м²
	плинтус		**K15**	NCS S 0300-N	Orac Decor · Contour (Luxxus)	полуматов.		92	7,9 м
10. Холл второго этажа 15,51 м²	стены		**K1**	Tikkurila G503	Farrow & Ball · Modern Emulsion	матовая	1	89	34,7 м²
	потолок		**K3**	Little Greene No. 222	Tikkurila · Anti-Reflex 2	глубокомат.	2	92	15,5 м²
	пол		**KM1**	по образцу	Coswick · Вековые традиции				15,5 м²
	плинтус		**K4**	Tikkurila G503	МДФ · в цвет Tikkurila			89	11,1 м
11. Коридор второго этажа 5,16 м²	стены		**K1**	Tikkurila G503	Farrow & Ball · Modern Emulsion	матовая	1	89	19,3 м²
	потолок		**K3**	Little Greene No. 222	Tikkurila · Anti-Reflex 2	глубокомат.	2	92	5,2 м²
	пол		**KM1**	по образцу	Coswick · Вековые традиции				5,2 м²
	плинтус		**K4**	Tikkurila G503	МДФ · в цвет Tikkurila			89	5,7 м
12. Детская вторая 9,23 м²	стены		**K1**	Tikkurila G503	Farrow & Ball · Modern Emulsion	матовая	1	89	24,1 м²
	акцент А		**K16**	Tikkurila H440	Farrow & Ball · Modern Emulsion	матовая	1	≈51	7,4 м²
	потолок		**K3**	Little Greene No. 222	Tikkurila · Anti-Reflex 2	глубокомат.	2	92	9,2 м²
	пол		**KM1**	по образцу	Coswick · Вековые традиции				9,2 м²
	плинтус		**K10**	Tikkurila G503	Orac Decor · Contour (Luxxus)			89	11,4 м
13. Санузел второго этажа 5,31 м²	стены		**K6**	Atlas Concorde A8UZ	Atlas Concorde · Marvel Travertine				19,1 м²
	потолок		**K7**	Little Greene No. 222	Tikkurila · Luja 7	матовая	1	92	5,3 м²
	пол		**K6**	Atlas Concorde A8UZ	Atlas Concorde · Marvel Travertine				5,3 м²

Условные обозначения

- **K1** Tikkurila G503 · Calla · Modern Emulsion · матовая · кл. 1
- **K2** NCS S 3050-R80B · Эгейский синий · Farrow & Ball Modern Emulsion · матовая · кл. 1
- **K3** Little Greene No. 222 · Loft White · Anti-Reflex 2 · глубокомат. · кл. 2
- **K4** Tikkurila G503 · Calla · МДФ
- **K5** NCS S 5020-G90Y · Олива · Farrow & Ball Modern Emulsion · матовая · кл. 1
- **K6** Atlas Concorde A8UZ · Marvel Travertine · Marvel Travertine
- **K7** Little Greene No. 222 · Loft White · Luja 7 · матовая · кл. 1
- **K8** Farrow & Ball No. 89 · Lulworth Blue — светлая морская лазурь · Modern Emulsion · матовая · кл. 1
- **K9** Farrow & Ball No. 66 · India Yellow — охра / горчица итальянских фасадов · Modern Emulsion · матовая · кл. 1
- дерево (доска, паркет, ламинат) — рисунок досок
- керамогранит, плитка, камень — сетка швов по формату
- HEX не задан — цвет только по коду и вееру
- **K10** Tikkurila G503 · Calla · Contour (Luxxus)
- **K11** Little Greene No. 222 · Loft White · Harmony · матовая · кл. 1
- **K12** Little Greene No. 222 · Loft White · МДФ
- **K13** NCS S 0502-Y · Tikkurila · матовая · кл. 2
- **K14** NCS S 0300-N · Tikkurila · глубокомат. · кл. 2
- **K15** NCS S 0300-N · Orac Decor Contour (Luxxus) · полуматов.
- **K16** Tikkurila H440 · H440 Wave — бирюзово-голубая вода · Modern Emulsion · матовая · кл. 1
- **KM1** инженерная доска · 1167-4250
- **KM2** аналог: керамогранит под травертин, матовый, 1200×600×9 мм

К — позиция окраски (код + продукт + блеск), КМ — позиция материала, тон КМ — по описанию артикула, эталон — образец материала; ≈ LRV — расчёт по HEX, справочно

Допущения и предложения на листе

Основа листа: взаимное расположение помещений, контур дома 9600 × 8000 и раскладка этажей подобраны проектировщиком под габариты помещений брифа; обмер и проект АР — задание (К-1); высота потолка 2900 мм — по брифу, не замерена; перекрытие 330 мм и отметка 2-го этажа +3,230 приняты; проект КР — задание (К-2); наружные стены 400 мм, перегородки 120 мм приняты (в брифе толщин нет) (К-1); разрешённая мощность 15 кВт принята по типовым ТУ для частного дома (К-4).

Знак «**» — предложение проектировщика, заказчиком не утверждено (согласовать с заказчиком): записи в реестре нет: плинтус пом. 1–3, 5, 6, 8, 10, 11, фартук пом. 1 — артикул изделия не выбран: позиция описана характеристиками («аналог по характеристикам»), артикул выбирается при закупке.

См. лист открытых вопросов (лист 6, записи К-1, К-2, К-4).

Перечень выкрасов на согласование

№	Код	Бренд / веер	Пом. / стена	Подложка	Формат	Статус
1	G503	Tikkurila	1, 2, 3, 5, 6, 7, 10, 11, 12	ГКЛ, загрунтованный под эту краску; МДФ, загрунтованный под эмаль	600×1000; 300×600	к выполнению
2	S 3050-R80B	NCS Farrow & Ball	1 A	ГКЛ, загрунтованный под эту краску	600×1000	к выполнению
3	No. 222	Little Greene	1, 2, 3, 4, 5, 6, 7, 8, 10, 11, 12, 13	ГКЛ, загрунтованный под эту краску; МДФ, загрунтованный под эмаль	600×1000; 300×600	к выполнению
4	S 5020-G90Y	NCS Farrow & Ball	3 A	ГКЛ, загрунтованный под эту краску	600×1000	к выполнению
5	No. 89	Farrow & Ball	6 A	ГКЛ, загрунтованный под эту краску	600×1000	к выполнению
6	No. 66	Farrow & Ball	7 A	ГКЛ, загрунтованный под эту краску	600×1000	к выполнению
7	S 0502-Y	NCS Tikkurila	9	ГКЛ, загрунтованный под эту краску	600×1000	к выполнению
8	S 0300-N	NCS Tikkurila	9	ГКЛ, загрунтованный под эту краску; МДФ, загрунтованный под эмаль	600×1000; 300×600	к выполнению
9	H440	Tikkurila	12 A	ГКЛ, загрунтованный под эту краску	600×1000	к выполнению

Примечания

1. Цвет утверждается только по выкрасу на объекте: формат от А3 до 1000×1000 мм на загрунтованном ГКЛ, в 2 слоя (как на стене), не на белой шпаклёвке; смотреть днём и при свете проекта своего помещения, рядом с образцами пола и фасадов. Подпись на обороте: код, бренд и веер, дата.
2. Колеровка машинная в колеровочном центре бренда; каждый код — за один проход, одной партией на весь объём. Колеровщику передаётся только система и код утверждённого веера; плашки и HEX на листе — ориентир, печать не является эталоном цвета.
3. Класс мокрого истирания — EN 13300 (ISO 11998); блеск — по ГОСТ 31975 (ISO 2813), геометрия 60°. LRV — пересчёт координаты L* каталога производителя (Y = ((L*+16)/116)³); «≈» — расчёт по HEX, справочно.
4. Площади поверхностей — тем же способом и с теми же цифрами, что в ведомости отделки (способ счёта — в общих указаниях); объём краски к заказу, фасовка и материалы КМ — в спецификации отделочных материалов.
5. Перечень выкрасов составлен по кодам колерной карты; к основному тону стен добавить на выкрас 2 соседних тона того же веера (светлее и темнее), статус отмечать в графе «Статус» при согласовании.
6. Колерная карта на 2 листах: обозначения повторены на каждом, схема квартиры и палитра — на первом, перечень выкрасов — на последнем.

Изм.	Кол.уч	Лист	№ док.	Подп.	Дата
Разраб.		Кырлан А.С.			19.10.26
Пров.					
ГИП					
Н. контр.					
Утв.					

ГД-2026-012-АИ

Дом 120 м²

Общая площадь 147,36* м² · * размеры приняты, не замерены (реестр — л. 6, К-1)

Дизайн-проект интерьера

Стадия	Лист	Листов
РП	64	130

Колерная карта

М б/м

Кырлан Александр Сергеевич

выпуск 19.10.2026 № 53e4f7ddae · стр. 68 из 160

Спецификация отделочных материалов

ПРЕДВАРИТЕЛЬНО · не для производства работ · открыто пунктов: 6 (реестр — л. 6)

Форма 1 по ГОСТ 21.110-2013 · количества — из геометрии проекта, с запасом · часть 1 из 2

Поз.	Наименование и техническая характеристика	Тип, марка, обозначение документа	Код продукции	Поставщик	Ед. изм.	Кол.	Масса 1 ед., кг	Примечание
	Лакокрасочные материалы							
1	Краска интерьерная водно-дисперсионная акриловая для стен, матовая, класс мокрого истирания 1 по EN 13300, база A; цвет Tikkurila G503 «Calla», колеровка машинная	Farrow & Ball Modern Emulsion		Farrow & Ball	л	77,5		поз. К1 колерной карты; пом. 1, 2, 3, 5, 6, 7, 10, 11, 12; S = 284,9 м² × 2 сл. × 0,12 л/м² = 68,4 л, +10 % и 0,5 л на подкраску → ≥ 75,7 л; тара 15 × 5 л + 1 × 2,5 л
2	Краска интерьерная водно-дисперсионная акриловая для акцентных стен, матовая, класс мокрого истирания 1 по EN 13300, база C; цвет NCS S 3050-R80B «Эгейский синий», колеровка машинная	Farrow & Ball Modern Emulsion		Farrow & Ball	л	5		поз. К2 колерной карты; пом. 1; S = 11,6 м² × 2 сл. × 0,12 л/м² = 2,8 л, +10 % и 0,5 л на подкраску → ≥ 3,6 л; тара 1 × 5 л
3	Краска интерьерная водно-дисперсионная акриловая для потолков, глубокоматовая, класс мокрого истирания 2 по EN 13300, база A; цвет Little Greene No. 222 «Loft White», колеровка машинная	Tikkurila Anti-Reflex 2		Tikkurila	л	36		поз. К3 колерной карты; пом. 1, 2, 3, 5, 6, 7, 8, 10, 11, 12; S = 133,2 м² × 2 сл. × 0,12 л/м² = 32,0 л, +10 % и 0,5 л на подкраску → ≥ 35,7 л; тара 4 × 9 л
4	Краска интерьерная водно-дисперсионная акриловая для акцентных стен, матовая, класс мокрого истирания 1 по EN 13300, база C; цвет NCS S 5020-G90Y «Олива», колеровка машинная	Farrow & Ball Modern Emulsion		Farrow & Ball	л	5		поз. К5 колерной карты; пом. 3; S = 10,8 м² × 2 сл. × 0,12 л/м² = 2,6 л, +10 % и 0,5 л на подкраску → ≥ 3,4 л; тара 1 × 5 л
5	Краска интерьерная водно-дисперсионная акриловая для потолков, матовая, класс мокрого истирания 1 по EN 13300, база A; цвет Little Greene No. 222 «Loft White», колеровка машинная	Tikkurila Luja 7		Tikkurila	л	3,6		поз. К7 колерной карты; пом. 4, 13; S = 9,5 м² × 2 сл. × 0,12 л/м² = 2,3 л, +10 % и 0,5 л на подкраску → ≥ 3,0 л; тара 1 × 2,7 л + 1 × 0,9 л
6	Краска интерьерная водно-дисперсионная акриловая для акцентных стен, матовая, класс мокрого истирания 1 по EN 13300, база C; цвет Farrow & Ball No. 89 «Lulworth Blue — светлая морская лазурь», колеровка машинная	Farrow & Ball Modern Emulsion		Farrow & Ball	л	5		поз. К8 колерной карты; пом. 6; S = 8,1 м² × 2 сл. × 0,12 л/м² = 2,0 л, +10 % и 0,5 л на подкраску → ≥ 2,7 л; тара 1 × 5 л
7	Краска интерьерная водно-дисперсионная акриловая для акцентных стен, матовая, класс мокрого истирания 1 по EN 13300, база C; цвет Farrow & Ball No. 66 «India Yellow — охра / горчица итальянских фасадов», колеровка машинная	Farrow & Ball Modern Emulsion		Farrow & Ball	л	5		поз. К9 колерной карты; пом. 7; S = 10,8 м² × 2 сл. × 0,12 л/м² = 2,6 л, +10 % и 0,5 л на подкраску → ≥ 3,4 л; тара 1 × 5 л
8	Краска интерьерная водно-дисперсионная акриловая для стен, матовая, класс мокрого истирания 1 по EN 13300, база A; цвет Little Greene No. 222 «Loft White», колеровка машинная	Tikkurila Harmony		Tikkurila	л	7,2		поз. К11 колерной карты; пом. 8; S = 22,1 м² × 2 сл. × 0,12 л/м² = 5,3 л, +10 % и 0,5 л на подкраску → ≥ 6,3 л; тара 2 × 2,7 л + 2 × 0,9 л
9	Краска интерьерная водно-дисперсионная акриловая для стен, матовая, класс мокрого истирания 2 по EN 13300, база A; цвет NCS S 0502-Y, колеровка машинная	Tikkurila		Tikkurila	л	7,2		поз. К13 колерной карты; пом. 9; S = 23,6 м² × 2 сл. × 0,12 л/м² = 5,7 л, +10 % и 0,5 л на подкраску → ≥ 6,7 л; тара 2 × 2,7 л + 2 × 0,9 л
10	Краска интерьерная водно-дисперсионная для потолков, глубокоматовая, класс мокрого истирания 2 по EN 13300, база A; цвет NCS S 0300-N, колеровка машинная	Tikkurila		Tikkurila	л	1,8		поз. К14 колерной карты; пом. 9; S = 4,7 м² × 2 сл. × 0,12 л/м² = 1,1 л, +10 % и 0,5 л на подкраску → ≥ 1,7 л; тара 2 × 0,9 л
11	Краска интерьерная водно-дисперсионная акриловая для акцентных стен, матовая, класс мокрого истирания 1 по EN 13300, база C; цвет Tikkurila H440 «H440 Wave — бирюзово-голубая вода», колеровка машинная	Farrow & Ball Modern Emulsion		Farrow & Ball	л	2,5		поз. К16 колерной карты; пом. 12; S = 7,4 м² × 2 сл. × 0,12 л/м² = 1,8 л, +10 % и 0,5 л на подкраску → ≥ 2,5 л; тара 1 × 2,5 л
12	Краска для МДФ и дерева в цвет Tikkurila G503 «Calla» — окраска плинтуса; блеск не ниже блеска стен	марка не задана			л	2,9		поз. К4, К10; пом. 1, 2, 3, 5, 6, 7, 10, 11, 12; L = 116,5 м, S = 10,9 м² × 2 сл. × 0,12 л/м² + 10 %; продукт подобрать в веере Tikkurila
13	Краска для МДФ и дерева в цвет Little Greene No. 222 «Loft White» — окраска плинтуса; блеск не ниже блеска стен	марка не задана			л	0,5		поз. К12; пом. 8; L = 7,4 м, S = 0,7 м² × 2 сл. × 0,12 л/м² + 10 %; продукт подобрать в веере Little Greene
14	Акрил, полуматовая в цвет NCS S 0300-N — окраска плинтуса	аналог по характеристикам			л	0,5		поз. К15; пом. 9; L = 7,9 м, S = 0,7 м² × 2 сл. × 0,12 л/м² + 10 %; продукт подобрать в веере NCS
15	Грунтовка акриловая под окраску стен и потолков — из системы производителя краски	по системе краски			м²	527		площадь окраски стен, акцентов и потолков; 1 слой перед окраской; расход — по ТУ грунтовки

Допущения и предложения на листе

Основа листа: взаимное расположение помещений, контур дома 9600 × 8000 и раскладка этажей подобраны проектировщиком под габариты помещений брифа; обмер и проект АР — задание (К-1); высота потолка 2900 мм — по брифу, не замерена; перекрытие 330 мм и отметка 2-го этажа +3,230 приняты; проект КР — задание (К-2); наружные стены 400 мм, перегородки 120 мм приняты (в брифе толщин нет) (К-1); разрешённая мощность 15 кВт принята по типовым ТУ для частного дома (К-4).

Знак «**» — предложение проектировщика, заказчиком не утверждено (согласовать с заказчиком): записи в реестре нет: плинтус пом. 1–3, 5, 6, 8, 10, 11, фартук пом. 1 — артикул изделия не выбран: позиция описана характеристиками («аналог по характеристикам»), артикул выбирается при закупке.

См. лист открытых вопросов (лист 6, записи К-1, К-2, К-4).

Изм.	Кол.уч	Лист	№ док.	Подп.	Дата
Разраб.		Кырлан А.С.			19.10.26
Пров.					
ГИП					
Н. контр.					
Утв.					

ГД-2026-012-АИ

Дом 120 м²

Общая площадь 147,36* м² · * размеры приняты, не замерены (реестр — л. 6, К-1)

Дизайн-проект интерьера	Стадия	Лист	Листов
	РП	65	130
Спецификация отделочных материалов М б/м	**Кырлан Александр Сергеевич**		

Спецификация отделочных материалов

ПРЕДВАРИТЕЛЬНО · не для производства работ · открыто пунктов: 6 (реестр — л. 6)

Форма 1 по ГОСТ 21.110-2013 · количества — из геометрии проекта, с запасом · часть 2 из 2

Поз.	Наименование и техническая характеристика	Тип, марка, обозначение документа	Код продукции	Поставщик	Ед. изм.	Кол.	Масса 1 ед., кг	Примечание
	Плитка и керамогранит							
16	Керамогранит под травертин, 600×600 мм	аналог по характеристикам			м²	14,04		шов 2 мм; Санузел гостевой, пол; Санузел второго этажа, пол; по раскладке 35 шт (S = 9,48 м²), с запасом 39 шт
17	Керамогранит под травертин, 600×1200×9 мм, ректификат, водопоглощение 0,1 %	аналог по характеристикам		Atlas Concorde	м²	63,36		шов 2 мм; Санузел гостевой, стены А–Г; Санузел гостевой, короб инсталляции; Санузел второго этажа, стены А–Г; Санузел второго этажа, короб инсталляции; по раскладке 78 шт (S = 38,01 м²), с запасом 88 шт
18	A8UZ, 600×1200×9 мм, ректификат, водопоглощение 0,1 % (BIa), противоскольжение R10, PEI IV	A8UZ		Atlas Concorde	м²	14,40		шов 2 мм; Прихожая, пол; по раскладке 18 шт (S = 12,20 м²), с запасом 20 шт
19	Керамогранит под травертин, матовый, 1200×600×9 мм, ректификат, водопоглощение 0,1 % (BIa)	аналог по характеристикам			м²	5,04		шов 2 мм; Гостиная-кухня, фартук (ст. А); Гостиная-кухня, фартук (ст. Б); по раскладке 5 шт (S = 2,00 м²), с запасом 7 шт
	Напольные покрытия							
20	1167-4250, рабочий слой 4 мм, эмиссия E1, укладка на клей	1167-4250		Coswick	м²	129,5		пом. 1, 2, 3, 6, 7, 8, 10, 11, 12; S = 121,02 м² + 7 % (прямая укладка); к заказу — кратно упаковке
21	1167-4250, класс 33, рабочий слой 4 мм, эмиссия E1, укладка на клей	1167-4250		Coswick	м²	5		пом. 9; S = 4,66 м² + 7 % (прямая укладка); к заказу — кратно упаковке
22	Клей для паркета и инженерной доски, эластичный (СМП / полиуретановый)	по рекомендации производителя доски			м²	126		площадь приклейки; расход и шпатель — по ТУ клея
	Погонажные изделия							
23	Плинтус МДФ под покраску 80×16, крепление к стене, окраска в цвет Tikkurila G503	аналог по характеристикам			м	110		пом. 1, 2, 3, 5, 6, 8, 10, 11; L = 99,3 м (периметр без дверных проёмов) + 10 % на подрезку; в штуках — по длине планки
24	SX165, h = 69 мм, крепление к стене, окраска в цвет Tikkurila G503	SX165		Orac Decor	м	36		пом. 7, 9, 12; L = 32,5 м (периметр без дверных проёмов) + 10 % на подрезку; в штуках — по длине планки
	Смеси и материалы для облицовки							
25	Затирка для швов плитки, класс CG2WA по EN 13888	Mapei Ultracolor Plus 132		Mapei	кг	5		по раскладке (a+b)/(a·b) × шов × t × 1,6 + 10 %; в т. ч. 0,9 кг — позиции раскладки без марки
26	Клей плиточный C2 TE S1 по EN 12004, слой 5 мм	Ceresit CM 17		Ceresit	кг	493		20 меш. по 25 кг; 1,5 кг/м² на 1 мм слоя + 10 %; в т. ч. 92 кг — позиции раскладки без марки
27	Гидроизоляция обмазочная мокрых зон: пол, стены по периметру, зоны замачивания; 2 слоя с армирующей лентой в углах	аналог по характеристикам			м²	19,6		площадь по листу раскладки плитки + 10 %; расход смеси — по ТУ
28	Лента демпферная по периметру пола из плитки	аналог по характеристикам			м	27,6		периметр без дверных проёмов + 10 %

Примечания

1. Количества — из геометрии проекта: площади поверхностей по чистым граням стен до отделки (те же, что в ведомости отделки и колерной карте), плитка, клей и затирка — по раскладке плиточника; в графе «Кол.» — к заказу, с запасом.
2. Краска: расход 0,12 л/м² на слой в 2 слоя, если по ТУ не задан иной; запас 10 % и 0,5 л на подкраску каждого кода. Один код — одна партия, колеровка машинная в колеровочном центре бренда; в заказ — только после утверждения выкраса (колерная карта). Фасовка — по каталогу бренда на дату выпуска; к заказу — не меньше расчётного объёма.
3. «Аналог по характеристикам» — допускается изделие другого производителя с характеристиками не ниже указанных, по согласованию с автором проекта.
4. Графы «Код продукции» и «Масса 1 ед.» не заполнены: коды по классификатору продукции не присвоены, масса единицы до 25 кг (ГОСТ 21.110-2013).
5. Грунтовка и клей для доски указаны площадью обработки; объём — по ТУ выбранного продукта.

Допущения и предложения на листе

Основа листа: взаимное расположение помещений, контур дома 9600 × 8000 и раскладка этажей подобраны проектировщиком под габариты помещений брифа; обмер и проект АР — задание (К-1); высота потолка 2900 мм — по брифу, не замерена; перекрытие 330 мм и отметка 2-го этажа +3,230 приняты; проект КР — задание (К-2); наружные стены 400 мм, перегородки 120 мм приняты (в брифе толщин нет) (К-1); разрешённая мощность 15 кВт принята по типовым ТУ для частного дома (К-4).

Знак «**» — предложение проектировщика, заказчиком не утверждено (согласовать с заказчиком): записи в реестре нет: плинтус пом. 1–3, 5, 6, 8, 10, 11, фартук пом. 1 — артикул изделия не выбран: позиция описана характеристиками («аналог по характеристикам»), артикул выбирается при закупке.

См. лист открытых вопросов (лист 6, записи К-1, К-2, К-4).

Изм.	Кол.уч	Лист	№ док.	Подп.	Дата
Разраб.		Кырлан А.С.			19.10.26
Пров.					
ГИП					
Н. контр.					
Утв.					

ГД-2026-012-АИ

Дом 120 м²

Общая площадь 147,36* м² · * размеры приняты, не замерены (реестр — л. 6, К-1)

Дизайн-проект интерьера

Стадия	Лист	Листов
РП	66	130

Спецификация отделочных материалов

М б/м

Кырлан Александр Сергеевич

Концепция декора и визуализации

Средиземноморский · визуализации, палитра, материалы, ключевые предметы

Визуализация 1. Вид сверху (3D): планировка с мебелью, текстилем и декором

Расстановка — по плану мебели (лист 22); шторы, ковры, картины и растения — по плану текстиля и декора (лист 68).

Визуализация 15. Гостиная-кухня (пом. 1)

шторы Т13, Т14, Т15 · ковёр Т16 · картина ДК6 · растение ДК7, ДК40 · подушки, пледы Т17, Т18, Т19

Визуализация 4. Спальня родителей (пом. 6)

шторы Т1, Т2 · ковёр Т3 · картина ДК1 · растение ДК44 · подушки, пледы Т4, Т5, Т6

Визуализация 11. Детская (пом. 7)

шторы Т20, Т21 · ковёр Т22 · картина ДК2 · зеркало ДК4 · подушки, пледы Т23, Т24, Т25

Визуализация 13. Детская вторая (пом. 12)

шторы Т26, Т27 · ковёр Т28 · картина ДК10 · зеркало ДК11 · подушки, пледы Т29, Т30, Т31

Материалы и фактуры

Дуб натуральный

пол: пом. 1, 2, 3, 6, 7, 8, 9, 10, 11, 12; рамы ДК1, ДК2, ДК3,

Травертин (керамогранит)

пол и стены санузлов, фартук: пом. 1

Букле

подушки: Т10, Т17, Т23, Т29

Лён

портьеры, римская штора, подушки: Т1, Т4, Т7, Т13, Т15, Т20, Т26

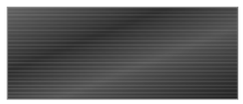

Чёрный матовый металл

рамы ДК4, ДК5, ДК11 — чёрный

Ключевые предметы

— Диван Гс2 2400×950 — гостиная-кухня; подушки и плед Т17, Т18, Т19

— Кровати Д1, Д6, М1 — над изголовьем картины ДК1, ДК2, ДК10; текстиль Т4, Т5, Т6, Т23, Т24, Т25, Т29, Т30, Т31

— Ковры Т3, Т9, Т16, Т22, Т28 — шерсть, на противоскользящей подложке

— Картины ДК1, ДК2, ДК3, ДК6, ДК10 — центр на высоте 875–1650 мм

— Зеркала в рост ДК4, ДК5, ДК11; над умывальниками ДК9, ДК12

— Шторы-волна Т1, Т7, Т13, Т20, Т26 (NCS S 1010-Y20R), тюль Т2, Т8, Т14, Т21, Т27 (Little Greene No. 222)

— Растение ДК7, ваза ДК8, растение ДК40, растение ДК41, растение ДК43, растение ДК44, растение ДК45, растение ДК46

Настроение

Средиземноморский 60 % + скандинавский (scandinavian.json) 40 %: дом у соснового бора, светлый и солнечный. Стены — кремовый белый Calla G503 и известковый Wimborne White No. 239, потолки — Loft White No. 222; второй план — светлый песок S 1010-Y20R, морская лазурь Lulworth Blue No. 89, серо-оливковая листва Treron No. 292; акценты — эгейский синий S 3050-R80B, охра India Yellow No. 66, олива S 5020-G90Y. По брифу: дерево — дуб табак (мебель, лестница), фурнитура и светильники — латунь, рамы и металл — тёплый графит; свет тёплый 2700–3000 K, фасады матовые. Настроение стиля: солнце и воздух, морская свежесть, неторопливость, тёплая простота, жизнь на террасе. Свет тёплый, 2700–3000 K.

Примечания

1. Визуализации — образ интерьера. Изделия, размеры, высоты подвеса и привязки — по чертежам (план текстиля и декора — лист 68; шторы и карнизы — лист 70; ведомость текстиля — лист 71; ведомость декора и развеска — лист 73); при расхождении действуют чертежи и ведомости.
2. Коды цвета — ориентир подбора по веерам производителей; ткань утверждается по образцу при дневном свете и при свете проекта 2700–3000 K.
3. Мелкий стайлинг на визуализациях (книги, посуда, свечи) в ведомости не входит и поставляется заказчиком по желанию.

Палитра 60/30/10 и цвета текстиля

- Tikkurila G503 (Calla), LRV 89 — 60 % база
- Little Greene No. 222 (Loft White), LRV 92 — 60 % база — Т2, Т8, Т14, Т21, Т27
- Farrow & Ball No. 89 (Lulworth Blue — светлая морская лазурь), LRV 45 — 30 % второй цвет — Т5, Т6
- NCS S 3050-R80B (Эгейский синий), LRV 13 — 10 % акцент — Т18
- NCS S 5020-G90Y (Олива), LRV 20 — 10 % акцент — Т11, Т12
- Farrow & Ball No. 239 (Wimborne White — белый с каплей тёплой охры), LRV 89 — 60 % база
- NCS S 1010-Y20R (Светлый песок / известняк), LRV 75 — 30 % второй цвет — Т1, Т4, Т7, Т10, Т13, Т17, Т20, Т23, Т26, Т29
- Farrow & Ball No. 292 (Treron — серо-оливковая листва), LRV 15 — 30 % второй цвет
- Farrow & Ball No. 66 (India Yellow — охра / горчица итальянских фасадов), LRV 36 — 10 % акцент — Т24, Т25
- Tikkurila X463, LRV 51 — текстиль — Т9, Т15, Т16, Т19, Т22, Т28

Допущения и предложения на листе

Основа листа: взаимное расположение помещений, контур дома 9600 × 8000 и раскладка этажей подобраны проектировщиком под габариты помещений брифа; обмер и проект АР — задание (К-1); высота потолка 2900 мм — по брифу, не замерена; перекрытие 330 мм и отметка 2-го этажа +3,230 приняты; проект КР — задание (К-2); наружные стены 400 мм, перегородки 120 мм приняты (в брифе толщин нет) (К-1); разрешённая мощность 15 кВт принята по типовым ТУ для частного дома (К-4).
См. лист открытых вопросов (лист 6, записи К-1, К-2, К-4).

Изм.	Кол.уч	Лист	№ док.	Подп.	Дата
Разраб.		Кырлан А.С.			19.10.26
Пров.					
ГИП					
Н. контр.					
Утв.					

ГД-2026-012-АИ

Дом 120 м²

Общая площадь 147,36* м² · * размеры приняты, не замерены (реестр — л. 6, К-1)

Дизайн-проект интерьера

Стадия	Лист	Листов
РП	67	130

Концепция декора и визуализации

М б/м

Кырлан Александр Сергеевич

выпуск 19.10.2026 № 53e4f7ddae · стр. 71 из 160

План текстиля и декора · 1-й этаж

Шторы и карнизы, ковры, картины и зеркала, растения · размеры в мм от чистовых стен и чистого пола · марки — по ведомостям

ПРЕДВАРИТЕЛЬНО · не для производства работ · открыто пунктов: 6 (реестр — л. 6)

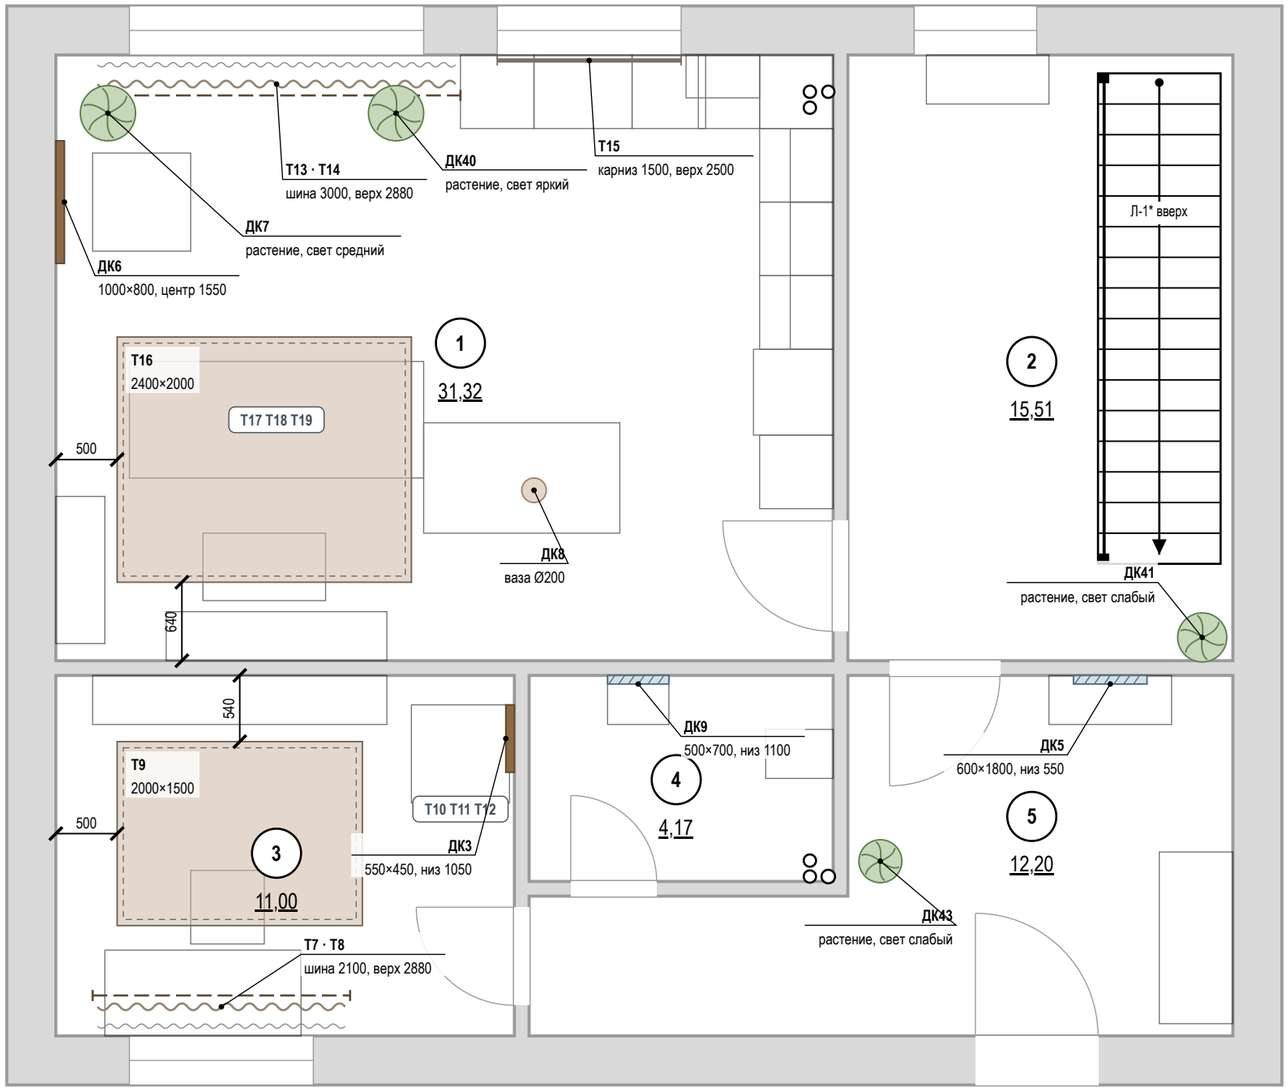

Условные обозначения

- ковёр — габарит в масштабе, цвет изделия
- шина или карниз штор (выше плоскости разреза)
- портьеры (штора-волна)
- тюль (на плане — волнистая линия)
- римская или рулонная штора в проёме
- картина на стене — ширина в масштабе
- зеркало на стене — ширина в масштабе
- растение в кашпо — диаметр в масштабе
- ваза, настольный декор
- подушки, пледы — марки на мебели
- привязка от чистовой стены, мм
- (1) номер помещения, площадь м²
- стены (подложка обмера)

Т1, ДК1 — марки по ведомостям текстиля и декора

Экспликация помещений

лист 13 · на плане — номера в марках

Окна: шина → полотно, мм

Поз.	Шина	Верх шины	Полотно, низ
Т13, Т14	3000	2880	2870, низ 10
Т15	1500	2500	1600, низ 900
Т7, Т8	2100	2880	2870, низ 10

Развеска: высоты от пола, мм

Поз.	Пом.	Ш×В	Центр	Низ	Стена
ДК3	3	550×450	1275	1050	Б
ДК5	5	600×1800	1450	550	А
ДК6	1	1000×800	1550	1150	Г
ДК9	4	500×700	1450	1100	А

Допущения и предложения на листе

Основа листа: взаимное расположение помещений, контур дома 9600 × 8000 и раскладка этажей подобраны проектировщиком под габариты помещений брифа; обмер и проект АР — задание (К-1); высота потолка 2900 мм — по брифу, не замерена; перекрытие 330 мм и отметка 2-го этажа +3,230 приняты; проект КР — задание (К-2); наружные стены 400 мм, перегородки 120 мм приняты (в брифе толщин нет) (К-1); разрешённая мощность 15 кВт принята по типовым ТУ для частного дома (К-4).
Знак «*» — принято, не замерено и не подтверждено (замерить на объекте): К-3: Л-1 — место, тип и размеры лестницы брифом не заданы (только «лестница из холла 1-го этажа»): одномаршевая 17 × 190 × 250 вдоль стены Б холла — предложение проектировщика; конструкция и расчёт — проект КР.
См. лист открытых вопросов (лист 6, записи К-1–К-4).

Примечания

1. Размеры — в мм. Отступы ковров — от чистовых стен; высоты картин и зеркал — от чистого пола до центра или низа рамы.
2. Шторы — на шинах в нишах потолка (ниша — план потолков, лист 52); закладная под шину — до обшивки ГКЛ. Схемы окон, длины полотен и сборка — лист 70.
3. Картины и зеркала массой более 5 кг — на анкеры по основанию, нагрузка крепежа не меньше двойной массы изделия; на ГКЛ — только по закладной. Декор не перекрывает розетки и выключатели.
4. Ковры на гладком полу — на противоскользящей подложке.
5. Мебель — по плану расстановки мебели (лист 22); ведомость текстиля — лист 71, ведомость декора и схемы развески — лист 73.
6. Номера помещений — по экспликации (лист 13); наименования и площади на этом листе не дублируются.
7. Марки текстиля «Т» и декора «Д» относятся только к листам текстиля и декора; индексы трубопроводов Т1–Т4 — на листах ВК и ОВ.

1000 мм · печать 1:1

Изм.	Кол.уч	Лист	№ док.	Подп.	Дата
Разраб.		Кырлан А.С.			19.10.26
Пров.					
ГИП					
Н. контр.					
Утв.					

ГД-2026-012-АИ

Дом 120 м²

Общая площадь 147,36* м² · * размеры приняты, не замерены (реестр — л. 6, К-1)

Дизайн-проект интерьера

Стадия	Лист	Листов
РП	68	130

План текстиля и декора · 1-й этаж

М 1:50

Кырлан Александр Сергеевич

выпуск 19.10.2026 № 53e4f7ddae · стр. 72 из 160

План текстиля и декора · 2-й этаж

Шторы и карнизы, ковры, картины и зеркала, растения · размеры в мм от чистовых стен и чистого пола · марки — по ведомостям

ПРЕДВАРИТЕЛЬНО · не для производства работ · открыто пунктов: 6 (реестр — л. 6)

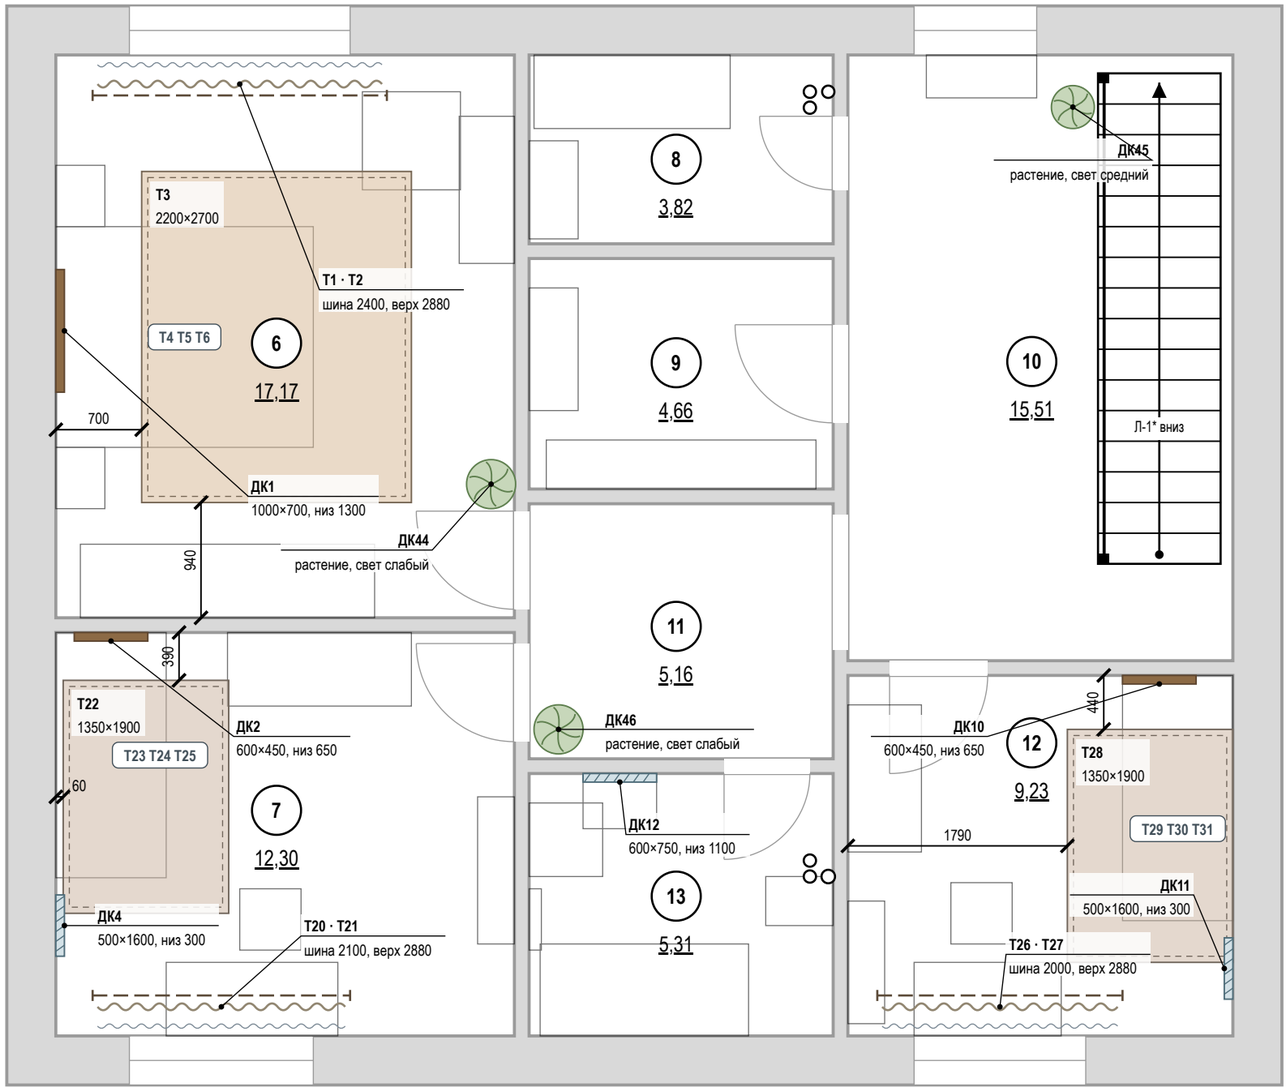

Условные обозначения

- ковёр — габарит в масштабе, цвет изделия
- шина или карниз штор (выше плоскости разреза)
- портьеры (штора-волна)
- тюль (на плане — волнистая линия)
- римская или рулонная штора в проёме
- картина на стене — ширина в масштабе
- зеркало на стене — ширина в масштабе
- растение в кашпо — диаметр в масштабе
- ваза, настольный декор
- подушки, пледы — марки на мебели
- привязка от чистовой стены, мм
- (1) номер помещения, площадь м²
- стены (подложка обмера)

Т1, ДК1 — марки по ведомостям текстиля и декора

Экспликация помещений

лист 13 · на плане — номера в марках

Окна: шина → полотно, мм

Поз.	Шина	Верх шины	Полотно, низ
Т1, Т2	2400	2880	2870, низ 10
Т20, Т21	2100	2880	2870, низ 10
Т26, Т27	2000	2880	2870, низ 10

Развеска: высоты от пола, мм

Поз.	Пом.	Ш×В	Центр	Низ	Стена
ДК1	6	1000×700	1650	1300	Г
ДК2	7	600×450	875	650	А
ДК4	7	500×1600	1100	300	Г
ДК10	12	600×450	875	650	А
ДК11	12	500×1600	1100	300	Б
ДК12	13	600×750	1475	1100	А

Допущения и предложения на листе. Основа листа: взаимное расположение помещений, контур дома 9600 × 8000 и раскладка этажей подобраны проектировщиком под габариты помещений брифа; обмер и проект АР — задание (К-1); высота потолка 2900 мм — по брифу, не замерена; перекрытие 330 мм и отметка 2-го этажа +3,230 приняты; проект КР — задание (К-2); наружные стены 400 мм, перегородки 120 мм приняты (в брифе толщин нет) (К-1); разрешённая мощность 15 кВт принята по типовым ТУ для частного дома (К-4). Знак «*» — принято, не замерено и не подтверждено (замерить на объекте): К-3: Л-1 — место, тип и размеры лестницы брифом не заданы (только «лестница из холла 1-го этажа»): одномаршевая 17 × 190 × 250 вдоль стены Б холла — предложение проектировщика; конструкция и расчёт — проект КР. См. лист открытых вопросов (лист 6, записи К-1–К-4).

Примечания

1. Размеры — в мм. Отступы ковров — от чистовых стен; высоты картин и зеркал — от чистого пола до центра или низа рамы.
2. Шторы — на шинах в нишах потолка (ниша — план потолков, лист 52); закладная под шину — до обшивки ГКЛ. Схемы окон, длины полотен и сборка — лист 70.
3. Картины и зеркала массой более 5 кг — на анкеры по основанию, нагрузка крепежа не меньше двойной массы изделия; на ГКЛ — только по закладной. Декор не перекрывает розетки и выключатели.
4. Ковры на гладком полу — на противоскользящей подложке.
5. Мебель — по плану расстановки мебели (лист 22); ведомость текстиля — лист 71, ведомость декора и схемы развески — лист 73.
6. Номера помещений — по экспликации (лист 13); наименования и площади на этом листе не дублируются.
7. Марки текстиля «Т» и декора «Д» относятся только к листам текстиля и декора; индексы трубопроводов Т1–Т4 — на листах ВК и ОВ.

1000 мм · печать 1:1

Изм.	Кол.уч	Лист	№ док.	Подп.	Дата
Разраб.		Кырлан А.С.			19.10.26
Пров.					
ГИП					
Н. контр.					
Утв.					

ГД-2026-012-АИ

Дом 120 м²

Общая площадь 147,36* м² · * размеры приняты, не замерены (реестр — л. 6, К-1)

Дизайн-проект интерьера

Стадия	Лист	Листов
РП	69	130

План текстиля и декора · 2-й этаж

М 1:50

Кырлан Александр Сергеевич

выпуск 19.10.2026 № 53e4f7ddae · стр. 73 из 160

03

Декор и текстиль

Кырлан Александр Сергеевич

выпуск 19.10.2026 · 53e4f7ddae · стр. 74 из 160

Шторы и карнизы

Схемы окон «шина → полотно» (М 1:100) · отметки от чистого пола помещения · размеры в мм

Окно 1 — Гостиная-кухня (пом. 1): Т13, Т14 (М 1:100)

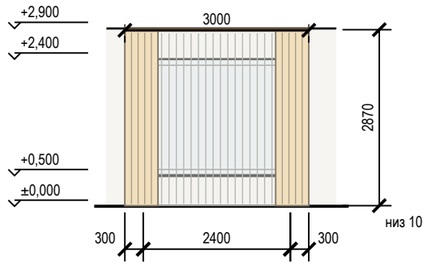

Окно 2 — Гостиная-кухня (пом. 1): Т15 (М 1:100)

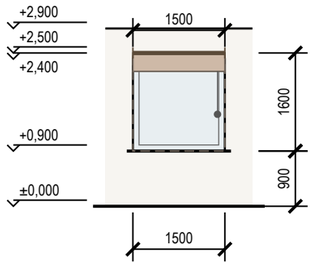

Окно 1 — Кабинет (пом. 3): Т7, Т8 (М 1:100)

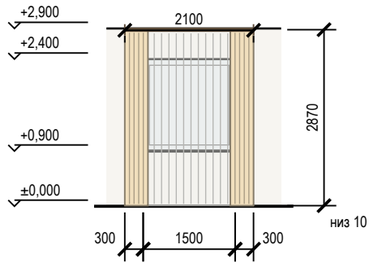

Окно 1 — Спальня родителей (пом. 6): Т1, Т2 (М 1:100)

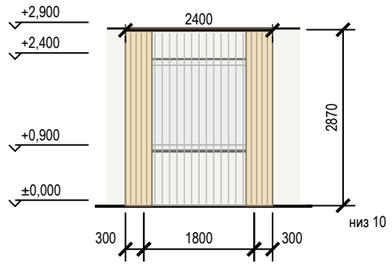

Окно 1 — Детская (пом. 7): Т20, Т21 (М 1:100)

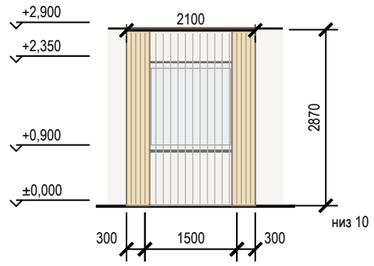

Окно 1 — Детская вторая (пом. 12): Т26, Т27 (М 1:100)

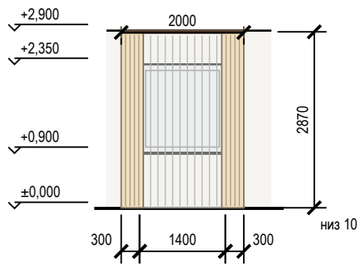

Задания смежникам

Кому	Задание	Пом.
Электрик	выводы под электрокарнизы не требуются (управление вручную)	

Условные обозначения

- портьеры в открытом положении
- римская штора: сложена / опущена
- верх ниши под шторы в потолке
- тюль (на виде окна — прозрачная плашка)
- шина или карниз на отметке верха
- оконный проём

Примечания

1. Отметки — от чистого пола помещения; размеры — мм. Длины полотен уточняются замером после чистовой отделки пола и потолка, до раскроя.
2. Карнизы — на анкеры по основанию; на ГКЛ — только по закладной.
3. Полотно портьер «парит» над полом на 10 мм; сборка портьер — 2,0, тюля — 2,5 (ширина полотна — в ведомости текстиля).
4. Шнур римской шторы — с натяжителем, петля низом не ниже 1500 мм от пола (защита детей; EN 13120 — рекомендация).
5. Электрокарнизы не предусмотрены; при замене на электропривод — вывод кабеля в нише у края шины (задание электрику).
6. Марки изделий — по плану текстиля и декора (лист 68) и ведомости текстиля (лист 71).

Допущения и предложения на листе

Основа листа: взаимное расположение помещений, контур дома 9600 × 8000 и раскладка этажей подобраны проектировщиком под габариты помещений брифа; обмер и проект АР — задание (К-1); высота потолка 2900 мм — по брифу, не замерена; перекрытие 330 мм и отметка 2-го этажа +3,230 приняты; проект КР — задание (К-2); наружные стены 400 мм, перегородки 120 мм приняты (в брифе толщин нет) (К-1); разрешённая мощность 15 кВт принята по типовым ТУ для частного дома (К-4).
См. лист открытых вопросов (лист 6, записи К-1, К-2, К-4).

Изм.	Кол.уч	Лист	№ док.	Подп.	Дата
Разраб.		Кырлан А.С.			19.10.26
Пров.					
ГИП					
Н. контр.					
Утв.					

ГД-2026-012-АИ

Дом 120 м²

Общая площадь 147,36* м² · * размеры приняты, не замерены (реестр — л. 6, К-1)

Дизайн-проект интерьера

Стадия	Лист	Листов
РП	70	130

Шторы и карнизы

М б/м

Кырлан Александр Сергеевич

выпуск 19.10.2026 № 53e4f7ddae · стр. 75 из 160

Ведомость текстиля

Шторы, тюль, римские шторы, ковры, подушки и пледы · размеры в мм · марки — по плану текстиля и декора

Текстиль: шторы, ковры, подушки, пледы

Поз.	Пом.	Изделие	Размер, мм	Ткань, состав, плотность	Сборка, ширина полотна		Цвет (система, код)	Кол.	Примечание
T1	6	Портьеры-волна	шина 2400 × полотно 2870	лён с блэкаут-подкладкой; лён 100 %; 320 г/м²	× 2, ширина 5000		NCS S 1010-Y20R (Светлый песок / известняк)	2	низ 10 (парит); на потолок
T2	6	Тюль	шина 2400 × полотно 2870	вуаль; полиэстер 100 %	× 2,5, ширина 6250		Little Greene No. 222 (Loft White)	1	низ 10 (парит); на потолок
T3	6	Ковёр под кроватью	2200×2700	шерсть, ручное ткачество; шерсть 80 %, хлопок 20 %			Tikkurila X395	1	противоскользящая подложка; ворс 10 мм
T4	6	Подушки декоративные на кровать	500×500	лён 100 %			NCS S 1010-Y20R (Светлый песок / известняк)	3	на М1
T5	6	Подушки на кровать, акцент	400×600	хлопковый бархат 100 %			Farrow & Ball No. 89 (Lulworth Blue — светлая морская лазурь)	2	на М1
T6	6	Плед на кровать	1300×1700	шерсть мериноса 100 %			Farrow & Ball No. 89 (Lulworth Blue — светлая морская лазурь)	1	на М1
T7	3	Портьеры-волна	шина 2100 × полотно 2870	лён с блэкаут-подкладкой; лён 100 %; 320 г/м²	× 2, ширина 3640		NCS S 1010-Y20R (Светлый песок / известняк)	2	низ 10 (парит); на потолок
T8	3	Тюль	шина 2100 × полотно 2870	вуаль; полиэстер 100 %	× 2,5, ширина 4550		Little Greene No. 222 (Loft White)	1	низ 10 (парит); на потолок
T9	3	Ковёр под кроватью	2000×1500	шерсть, плоское плетение; шерсть 100 %			Tikkurila X463	1	противоскользящая подложка; ворс 8 мм
T10	3	Подушки декоративные на кровать	500×500	букле (шерсть 60 %, полиэстер 40 %)			NCS S 1010-Y20R (Светлый песок / известняк)	3	на К64
T11	3	Подушки на кровать, акцент	400×600	хлопковый бархат 100 %			NCS S 5020-G90Y (Олива)	2	на К64
T12	3	Плед на кровать	1300×1700	шерсть мериноса 100 %			NCS S 5020-G90Y (Олива)	1	на К64
T13	1	Портьеры-волна (гостиная)	шина 3000 × полотно 2870	лён 70 %, вискоза 30 %; 280 г/м²	× 2, ширина 4500		NCS S 1010-Y20R (Светлый песок / известняк)	2	низ 10 (парит); на потолок
T14	1	Тюль (гостиная)	шина 3000 × полотно 2870	вуаль; полиэстер 100 %	× 2,5, ширина 5625		Little Greene No. 222 (Loft White)	1	низ 10 (парит); на потолок
T15	1	Римская штора (кухня)	карниз 1500 × полотно 1600	лён 100 %			Tikkurila X463	1	низ 900; на стену; шнур: петля 1500, натяжитель
T16	1	Ковёр в зоне отдыха	2400×2000	шерсть, петля; шерсть 100 %			Tikkurila X463	1	противоскользящая подложка; ворс низкий
T17	1	Подушки на диван	500×500	букле (шерсть 60 %, полиэстер 40 %)			NCS S 1010-Y20R (Светлый песок / известняк)	3	на Гс2
T18	1	Подушки на диван, акцент	400×600	хлопковый бархат 100 %			NCS S 3050-R80B (Эгейский синий)	2	на Гс2
T19	1	Плед на диван	1300×1700	альпака 50 %, шерсть 50 %			Tikkurila X463	1	на Гс2
T20	7	Портьеры-волна	шина 2100 × полотно 2870	лён с блэкаут-подкладкой; лён 100 %; 320 г/м²	× 2, ширина 3640		NCS S 1010-Y20R (Светлый песок / известняк)	2	низ 10 (парит); на потолок
T21	7	Тюль	шина 2100 × полотно 2870	вуаль; полиэстер 100 %	× 2,5, ширина 4550		Little Greene No. 222 (Loft White)	1	низ 10 (парит); на потолок
T22	7	Ковёр под кроватью	1350×1900	шерсть, плоское плетение; шерсть 100 %			Tikkurila X463	1	противоскользящая подложка; ворс 8 мм
T23	7	Подушки декоративные на кровать	500×500	букле (шерсть 60 %, полиэстер 40 %)			NCS S 1010-Y20R (Светлый песок / известняк)	3	на Д1
T24	7	Подушки на кровать, акцент	400×600	хлопковый бархат 100 %			Farrow & Ball No. 66 (India Yellow — охра / горчица итальянских фасадов)	2	на Д1
T25	7	Плед на кровать	1300×1700	шерсть мериноса 100 %			Farrow & Ball No. 66 (India Yellow — охра / горчица итальянских фасадов)	1	на Д1
T26	12	Портьеры-волна	шина 2000 × полотно 2870	лён с блэкаут-подкладкой; лён 100 %; 320 г/м²	× 2, ширина 3640		NCS S 1010-Y20R (Светлый песок / известняк)	2	низ 10 (парит); на потолок
T27	12	Тюль	шина 2000 × полотно 2870	вуаль; полиэстер 100 %	× 2,5, ширина 4550		Little Greene No. 222 (Loft White)	1	низ 10 (парит); на потолок
T28	12	Ковёр под кроватью	1350×1900	шерсть, плоское плетение; шерсть 100 %			Tikkurila X463	1	противоскользящая подложка; ворс 8 мм
T29	12	Подушки декоративные на кровать	500×500	букле (шерсть 60 %, полиэстер 40 %)			NCS S 1010-Y20R (Светлый песок / известняк)	3	на Д6
T30	12	Подушки на кровать, акцент	400×600	хлопковый бархат 100 %			Tikkurila H440	2	на Д6

Продолжение ведомости — на следующем листе; итог и примечания — на последнем листе ведомости.

Допущения и предложения на листе

Основа листа: взаимное расположение помещений, контур дома 9600 × 8000 и раскладка этажей подобраны проектировщиком под габариты помещений брифа; обмер и проект АР — задание (К-1); высота потолка 2900 мм — по брифу, не замерена; перекрытие 330 мм и отметка 2-го этажа +3,230 приняты; проект КР — задание (К-2); наружные стены 400 мм, перегородки 120 мм приняты (в брифе толщин нет) (К-1); разрешённая мощность 15 кВт принята по типовым ТУ для частного дома (К-4).
См. лист открытых вопросов (лист 6, записи К-1, К-2, К-4).

Изм.	Кол.уч	Лист	№ док.	Подп.	Дата
Разраб.		Кырлан А.С.			19.10.26
Пров.					
ГИП					
Н. контр.					
Утв.					

ГД-2026-012-АИ

Дом 120 м²

Общая площадь 147,36* м² · * размеры приняты, не замерены (реестр — л. 6, К-1)

Дизайн-проект интерьера

Стадия	Лист	Листов
РП	71	130

Ведомость текстиля

М б/м

Кырлан Александр Сергеевич

выпуск 19.10.2026 № 53e4f7ddae · стр. 76 из 160

Ведомость текстиля (продолжение)

Шторы, тюль, римские шторы, ковры, подушки и пледы · размеры в мм · марки — по плану текстиля и декора

Текстиль: шторы, ковры, подушки, пледы (продолжение)

Поз.	Пом.	Изделие	Размер, мм	Ткань, состав, плотность	Сборка, ширина полотна		Цвет (система, код)	Кол.	Примечание
T31	12	Плед на кровать	1300×1700	шерсть мериноса 100 %			Tikkurila H440	1	на Д6

образец цвета — по HEX производителя краски, справочно

Итого: шторы и тюль — 16 шт.; ковры и дорожки — 5 шт.; подушки, пледы, покрывала — 30 шт.

Образцы по помещениям

1. Гостиная-кухня

T13 T14 T15 T16 T17 T18 T19

3. Кабинет

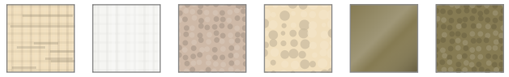

T7 T8 T9 T10 T11 T12

6. Спальня родительей

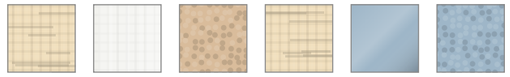

T1 T2 T3 T4 T5 T6

7. Детская

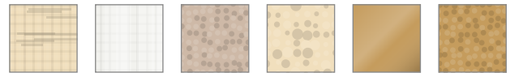

T20 T21 T22 T23 T24 T25

Примечания

1. Коды цвета — ориентир подбора по веерам производителей красок; ткань утверждается по образцу при дневном свете и при свете проекта 2700–3000 K.
2. Размеры полотен — по замеру после чистовой отделки пола и потолка; ширина полотна указана с учётом сборки, без припусков на швы. Схемы окон и отметки шин лист 70.
3. Портьеры и тюль — на тесьме «волна» по системе шины; блэкаут — подкладкой. Ковры — на противоскользящей подложке.
4. Замена изделия — аналогом по характеристикам (состав, плотность, размер, цвет по образцу) с согласованием автора проекта.
5. Места изделий — план текстиля и декора (лист 68); подушки и пледы — по марке мебели.

Допущения и предложения на листе

Основа листа: взаимное расположение помещений, контур дома 9600 × 8000 и раскладка этажей подобраны проектировщиком под габариты помещений брифа; обмер и проект АР — задание (К-1); высота потолка 2900 мм — по брифу, не замерена; перекрытие 330 мм и отметка 2-го этажа +3,230 приняты; проект КР — задание (К-2); наружные стены 400 мм, перегородки 120 мм приняты (в брифе толщин нет) (К-1); разрешённая мощность 15 кВт принята по типовым ТУ для частного дома (К-4).
См. лист открытых вопросов (лист 6, записи К-1, К-2, К-4).

Изм.	Кол.уч	Лист	№ док.	Подп.	Дата
Разраб.		Кырлан А.С.			19.10.26
Пров.					
ГИП					
Н. контр.					
Утв.					

ГД-2026-012-АИ

Дом 120 м²

Общая площадь 147,36* м² · * размеры приняты, не замерены (реестр — л. 6, К-1)

Дизайн-проект интерьера

Стадия	Лист	Листов
РП	72	130

Ведомость текстиля (продолжение)

М б/м

Кырлан Александр Сергеевич

выпуск 19.10.2026 № 53e4f7ddae · стр. 77 из 160

Ведомость декора. Схемы развески

ПРЕДВАРИТЕЛЬНО · не для производства работ · открыто пунктов: 6 (реестр — л. 6)

Картины, зеркала, растения, настольный декор · схемы развески (М 1:100) · высоты — мм от чистого пола

Декор: картины, зеркала, растения, предметы

картина · зеркало · мебель под изделием

Поз.	Пом.	Предмет	Размер, мм	Место: стена, высота от пола, мм	Масса, кг	Крепёж и основание	Свет места, отделка	Кол.
ДК1	6	Картина над кроватью: Ветви оливы с плодами, акварель на тёплой бумаге	1000×700	стена Г, привязка 1750; низ 1300, центр 1650; над М1	4	подвес по основанию, 2 точки	рама — дуб	1
ДК2	7	Картина над кроватью: Парусники в бухте, детская иллюстрация, гуашь	600×450	стена А, привязка 150; низ 650, центр 875; над Д1	4	подвес по основанию, 2 точки	рама — дуб	1
ДК3	3	Картина над креслом: Старинная карта Эгейского моря, гравюра в паспарту	550×450	стена Б, привязка 240; низ 1050, центр 1275; над Кб4	4	подвес по основанию, 2 точки	рама — дуб	1
ДК4	7	Зеркало в рост в тонкой чёрной раме	500×1600	стена Г, привязка 2140; низ 300, центр 1100	12	анкер для пустотелых оснований, 4 шт.; основание: перегородка — определить обмером до монтажа; нагрузка 30 кг	рама — чёрный матовый металл	1
ДК5	5	Зеркало	600×1800	стена А, привязка 1840; низ 550, центр 1450	18	анкер, 4 шт.; основание: перегородка — определить обмером до монтажа; нагрузка 40 кг	рама — чёрный матовый металл	1
ДК6	1	Картина над креслом: Белые дома над бирюзовой бухтой, синие ставни, полдень; масло	1000×800	стена Г, привязка 700; центр 1550	6	анкер, 2 шт.; основание: перегородка — определить обмером до монтажа; нагрузка 15 кг		1
ДК7	1	Растение	450×450	напольное			свет средний	1
ДК8	1	Ваза керамическая с ветками на обеденном столе	200×350	на Кх15 (обеденный стол)				1
ДК9	4	Зеркало над умывальником, влагостойкое	500×700	стена А, привязка 640; низ 1100, центр 1450; над Cr2	4	подвес по основанию, 2 точки		1
ДК10	12	Картина над кроватью: Солнце и волны из цветных полукругов, детский принт	600×450	стена А, привязка 2240; низ 650, центр 875; над Д6	4	подвес по основанию, 2 точки	рама — дуб	1
ДК11	12	Зеркало в рост в тонкой чёрной раме	500×1600	стена Б, привязка 2140; низ 300, центр 1100	12	анкер для пустотелых оснований, 4 шт.; основание: перегородка — определить обмером до монтажа; нагрузка 30 кг	рама — чёрный матовый металл	1
ДК12	13	Зеркало над умывальником, влагостойкое	600×750	стена А, привязка 440; низ 1100, центр 1475	4	подвес по основанию, 2 точки		1
ДК40	1	Олива в кадке Ø450 у окна	450×450	напольное			свет яркий рассеянный	1
ДК41	2	Сансевиерия в кашпо Ø400 под лестницей	400×400	напольное			свет слабый	1
ДК43	5	Замиокулькас в кашпо Ø350	350×350	напольное			свет слабый	1
ДК44	6	Аглаонема в кашпо Ø400	400×400	напольное			свет слабый	1
ДК45	10	Хлорофитум в кашпо Ø350 у окна	350×350	напольное			свет средний	1
ДК46	11	Сансевиерия в кашпо Ø400	400×400	напольное			свет слабый	1

ДК1 — Спальня родителей (пом. 6), стена Г (М 1:100)

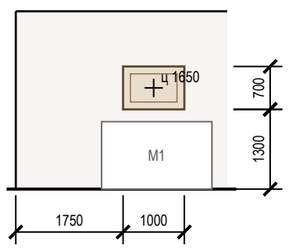

ДК2 — Детская (пом. 7), стена А (М 1:100)

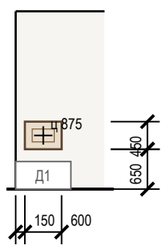

ДК3 — Кабинет (пом. 3), стена Б (М 1:100)

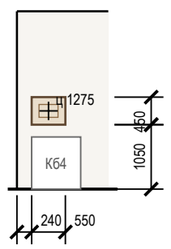

ДК4 — Детская (пом. 7), стена Г (М 1:100)

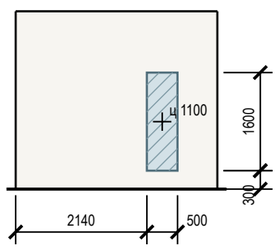

ДК5 — Прихожая (пом. 5), стена А (М 1:100)

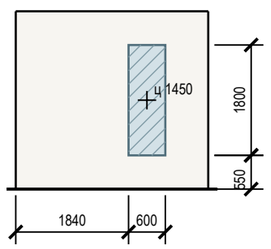

ДК6 — Гостиная-кухня (пом. 1), стена Г (М 1:100)

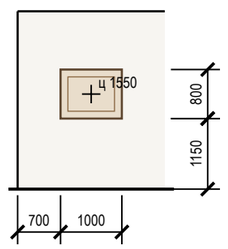

ДК9 — Санузел гостевой (пом. 4), стена А (М 1:100)

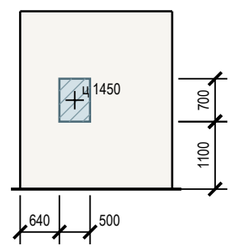

Допущения и предложения на листе

Основа листа: взаимное расположение помещений, контур дома 9600 × 8000 и раскладка этажей подобраны проектировщиком под габариты помещений брифа; обмер и проект АР — задание (К-1); высота потолка 2900 мм — по брифу, не замерена; перекрытие 330 мм и отметка 2-го этажа +3,230 приняты; проект КР — задание (К-2); наружные стены 400 мм, перегородки 120 мм приняты (в брифе толщин нет) (К-1); разрешённая мощность 15 кВт принята по типовым ТУ для частного дома (К-4).
См. лист открытых вопросов (лист 6, записи К-1, К-2, К-4).

Примечания

1. Высоты — от чистого пола помещения до низа изделия, «ц» — до центра; привязки — от чистовой грани угла стены, мм.
2. Над мебелью низ изделия — на 150–250 мм выше спинки или изголовья; без мебели центр — на 1450–1600 мм от пола.
3. Изделия до 5 кг — на два подвеса по основанию; тяжелее — на анкеры с нагрузкой не меньше двойной массы; на ГКЛ — только по закладной или анкеру для пустотелых оснований.
4. Зеркала в рост — с креплением от опрокидывания; в санузлах — влагостойкие, на клей для зеркал и нейтральный силикон.
5. Места изделий — план текстиля и декора (лист 68). Схемы ДК10, ДК11, ДК12 — по ведомости и плану.

Изм.	Кол.уч	Лист	№ док.	Подп.	Дата
Разраб.		Кырлан А.С.			19.10.26
Пров.					
ГИП					
Н. контр.					
Утв.					

ГД-2026-012-АИ

Дом 120 м²

Общая площадь 147,36* м² · * размеры приняты, не замерены (реестр — л. 6, К-1)

Дизайн-проект интерьера

Стадия	Лист	Листов
РП	73	130

Ведомость декора. Схемы развески

М б/м

Кырлан Александр Сергеевич

выпуск 19.10.2026 № 53e4f7ddae · стр. 78 из 160

Встроенная мебель. Схема расположения · 1-й этаж

встроенная и корпусная мебель на заказ, кухонный гарнитур · размеры в мм · марки — по ведомости изделий

ПРЕДВАРИТЕЛЬНО · не для производства работ · открыто пунктов: 6 (реестр — л. 6)

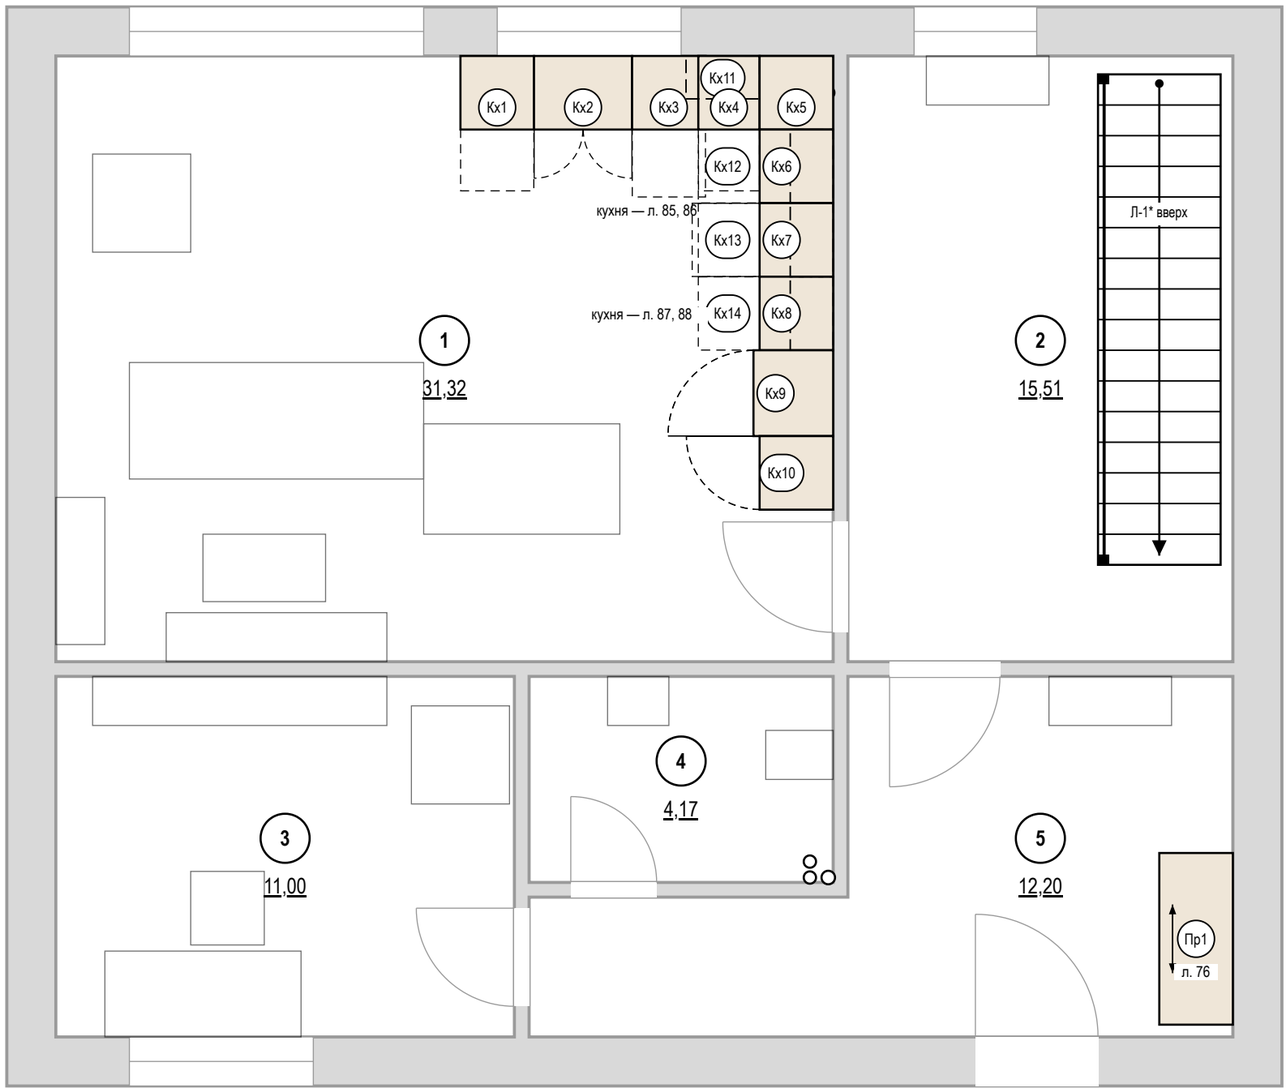

Ведомость изделий

Марка	Наименование	Пом.	Ш×Г×В, мм	Лист
Пр1	Шкаф-купе	5	1400×600×2800	76
Кх1	Модуль нижний: ящики	1	600×600×900	85
Кх2	Модуль нижний: мойка	1	800×600×900	85
Кх3	Модуль нижний: ПММ	1	600×600×900	85
Кх11	Модуль навесной: полки	1	600×350×900	85
Кх4	Модуль нижний: ящики	1	500×600×900	85
Кх5	Модуль нижний: ящики	1	600×600×900	85
Кх6	Модуль нижний: ящики	1	600×600×900	87
Кх12	Модуль навесной: полки	1	600×350×900	87
Кх7	Модуль нижний: духовой шкаф, варочная	1	600×600×900	87
Кх13	Модуль навесной: полки	1	600×350×900	87
Кх8	Модуль нижний: ящики	1	600×600×900	87
Кх14	Модуль навесной: полки	1	600×350×900	87
Кх9	Пенал: холодильник встр.	1	700×650×2200	87
Кх10	Пенал: полки	1	600×600×2200	87

Условные обозначения

- изделие мебельщика: корпус на полу
- навесной модуль (невидимый контур)
- открывание распашного фасада
- зона выдвижения ящика, двери техники
- дверь купе, стрелка — направление движения
- П5 — марка изделия, под ней — лист изделия

Допущения и предложения на листе

Основа листа: взаимное расположение помещений, контур дома 9600 × 8000 и раскладка этажей подобраны проектировщиком под габариты помещений брифа; обмер и проект АР — задание (К-1); высота потолка 2900 мм — по брифу, не замерена; перекрытие 330 мм и отметка 2-го этажа +3,230 приняты; проект КР — задание (К-2); наружные стены 400 мм, перегородки 120 мм приняты (в брифе толщин нет) (К-1); разрешённая мощность 15 кВт принята по типовым ТУ для частного дома (К-4).

Знак «*» — принято, не замерено и не подтверждено (замерить на объекте): К-3: Л-1 — место, тип и размеры лестницы брифом не заданы (только «лестница из холла 1-го этажа»): одномаршевая 17 × 190 × 250 вдоль стены Б холла — предложение проектировщика; конструкция и расчёт — проект КР.

См. лист открытых вопросов (лист 6, записи К-1–К-4).

Примечания

1. Изделия — по чистовым размерам помещений; перед раскроем — контрольный замер цеха после чистовой отделки стен, пола и потолка.
2. Открывание фасадов и выдвижение ящиков показано в открытом положении: зоны не пересекают двери, радиаторы, выключатели и проходы.
3. Стояки и счётчики за мебелью — с сервисным люком; газовые трубы мебелью не зашиваются.
4. Покупная мебель — по плану расстановки мебели и спецификации дизайнера; здесь — подложкой.

1000 мм · печать 1:1

Изм.	Кол.уч	Лист	№ док.	Подп.	Дата
Разраб.		Кырлан А.С.			19.10.26
Пров.					
ГИП					
Н. контр.					
Утв.					

ГД-2026-012-АИ

Дом 120 м²

Общая площадь 147,36* м² · * размеры приняты, не замерены (реестр — л. 6, К-1)

Дизайн-проект интерьера

Стадия	Лист	Листов
РП	74	130

Встроенная мебель. Схема расположения · 1-й этаж

М 1:50

Кырлан Александр Сергеевич

выпуск 19.10.2026 № 53e4f7ddae · стр. 79 из 160

Встроенная мебель. Схема расположения · 2-й этаж

встроенная и корпусная мебель на заказ, кухонный гарнитур · размеры в мм · марки — по ведомости изделий

ПРЕДВАРИТЕЛЬНО · не для производства работ · открыто пунктов: 6 (реестр — л. 6)

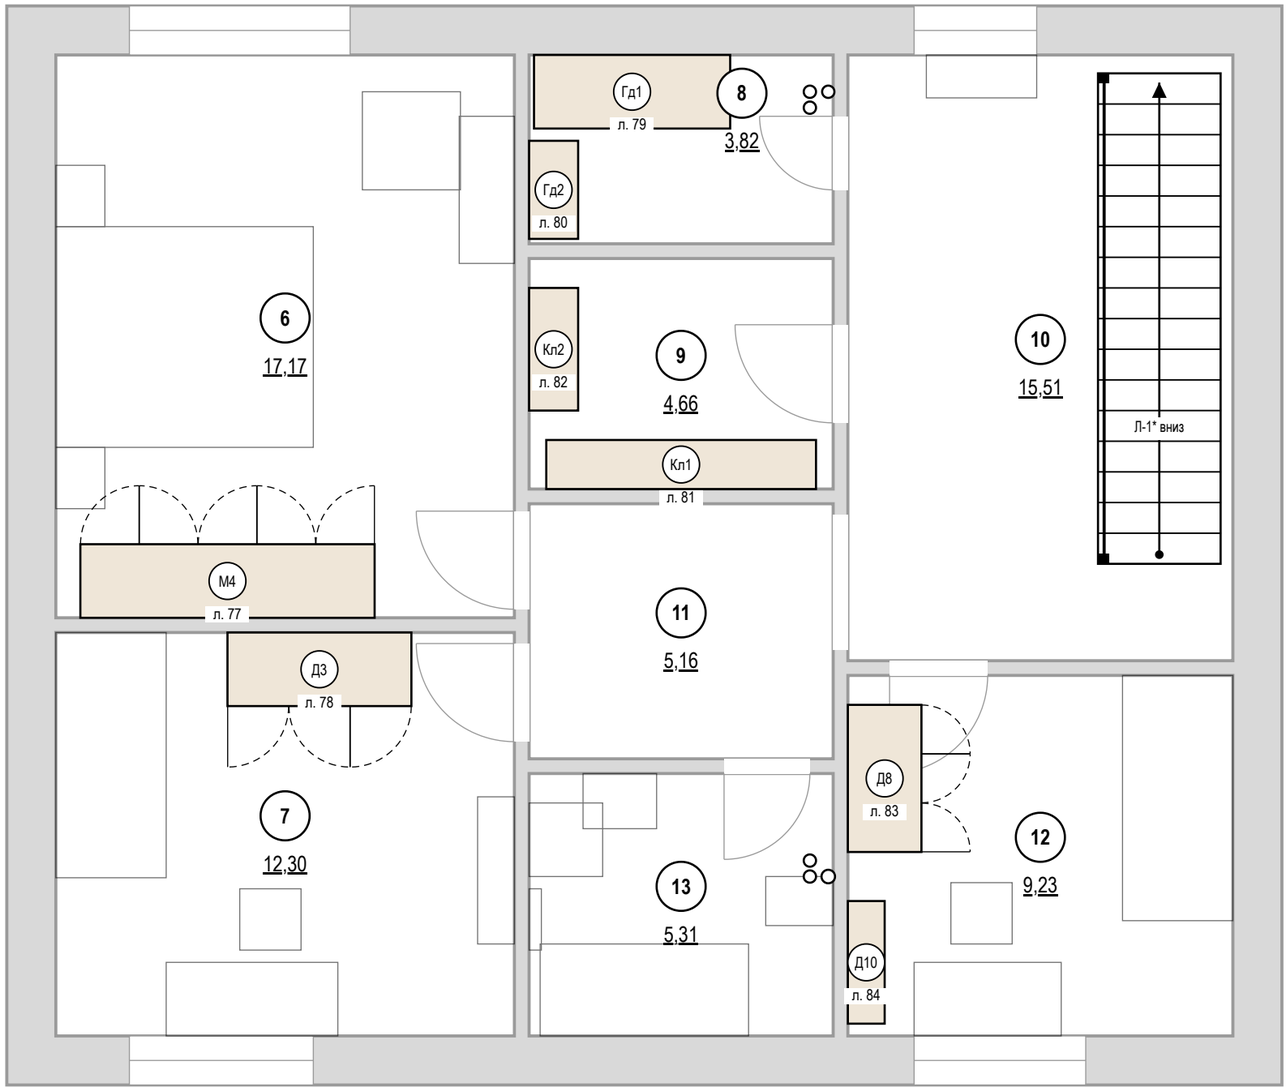

Ведомость изделий

Марка	Наименование	Пом.	Ш×Г×В, мм	Лист
М4	Шкаф распашной	6	2400×600×2600	77
Д3	Шкаф распашной	7	1500×600×2200	78
Гд1	Система хранения	8	1600×600×2600	79
Гд2	Система хранения	8	800×400×2000	80
Кл1	Система хранения	9	2200×400×2200	81
Кл2	Система хранения	9	1000×400×2200	82
Д8	Шкаф распашной	12	1200×600×2200	83
Д10	Система хранения	12	1000×300×1200	84

Условные обозначения

- изделие мебельщика: корпус на полу
- навесной модуль (невидимый контур)
- открывание распашного фасада
- зона выдвижения ящика, двери техники
- дверь купе, стрелка — направление движения
- П5 — марка изделия, под ней — лист изделия

Допущения и предложения на листе

Основа листа: взаимное расположение помещений, контур дома 9600 × 8000 и раскладка этажей подобраны проектировщиком под габариты помещений брифа; обмер и проект АР — задание (К-1); высота потолка 2900 мм — по брифу, не замерена; перекрытие 330 мм и отметка 2-го этажа +3,230 приняты; проект КР — задание (К-2); наружные стены 400 мм, перегородки 120 мм приняты (в брифе толщин нет) (К-1); разрешённая мощность 15 кВт принята по типовым ТУ для частного дома (К-4).

Знак «*» — принято, не замерено и не подтверждено (замерить на объекте): К-3: Л-1 — место, тип и размеры лестницы брифом не заданы (только «лестница из холла 1-го этажа»): одномаршевая 17 × 190 × 250 вдоль стены Б холла — предложение проектировщика; конструкция и расчёт — проект КР.

См. лист открытых вопросов (лист 6, записи К-1–К-4).

Примечания

1. Изделия — по чистовым размерам помещений; перед раскроем — контрольный замер цеха после чистовой отделки стен, пола и потолка.
2. Открывание фасадов и выдвижение ящиков показано в открытом положении: зоны не пересекают двери, радиаторы, выключатели и проходы.
3. Стояки и счётчики за мебелью — с сервисным люком; газовые трубы мебелью не зашиваются.
4. Покупная мебель — по плану расстановки мебели и спецификации дизайнера; здесь — подложкой.

1000 мм · печать 1:1

Изм.	Кол.уч	Лист	№ док.	Подп.	Дата
Разраб.		Кырлан А.С.			19.10.26
Пров.					
ГИП					
Н. контр.					
Утв.					

ГД-2026-012-АИ

Дом 120 м²

Общая площадь 147,36* м² · * размеры приняты, не замерены (реестр — л. 6, К-1)

Дизайн-проект интерьера

Стадия	Лист	Листов
РП	75	130

Встроенная мебель. Схема расположения · 2-й этаж

М 1:50

Кырлан Александр Сергеевич

Шкаф-купе Пр1

Прихожая (пом. 5) · вид из помещения · размеры в мм, отметки в м

ПРЕДВАРИТЕЛЬНО · не для производства работ · открыто пунктов: 6 (реестр — л. 6)

Вид с фасадами

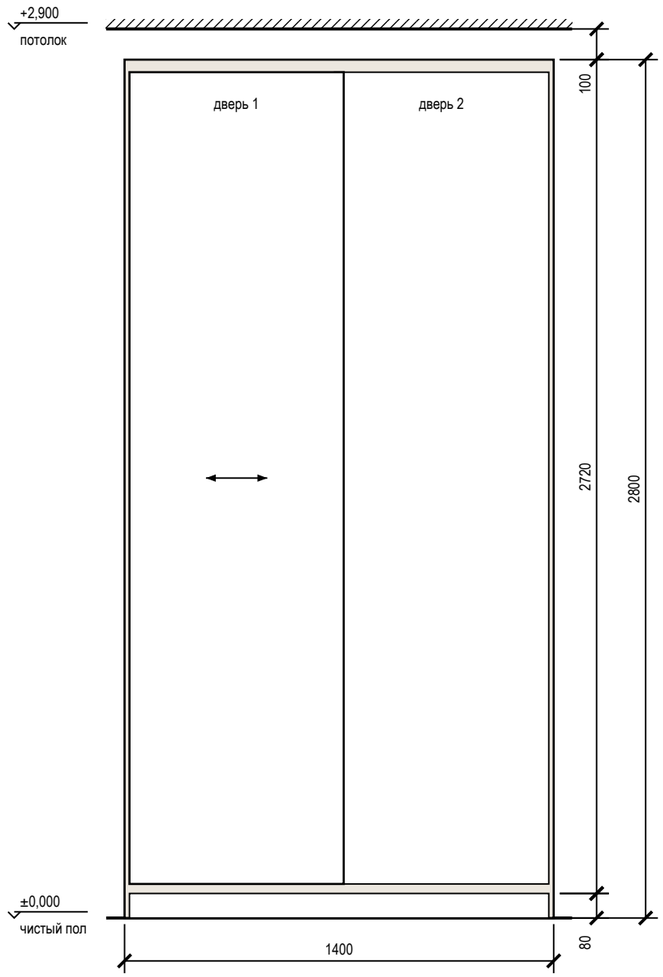

Вид без фасадов

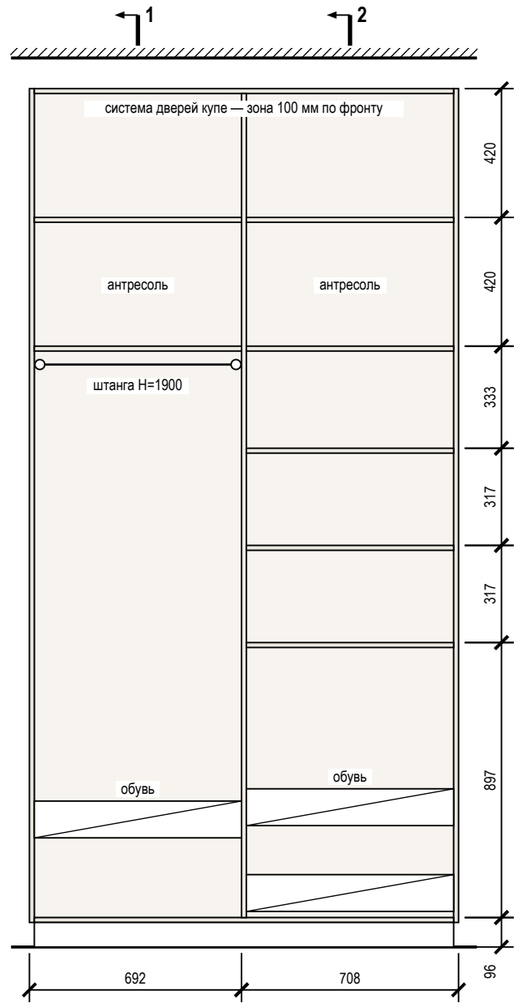

Разрез 1-1

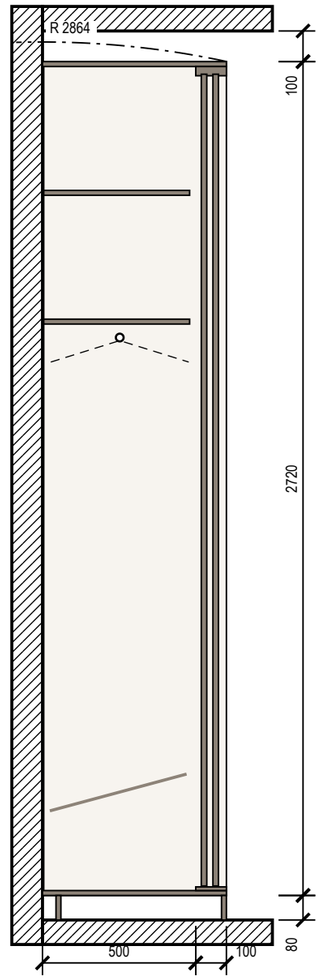

Разрез 2-2

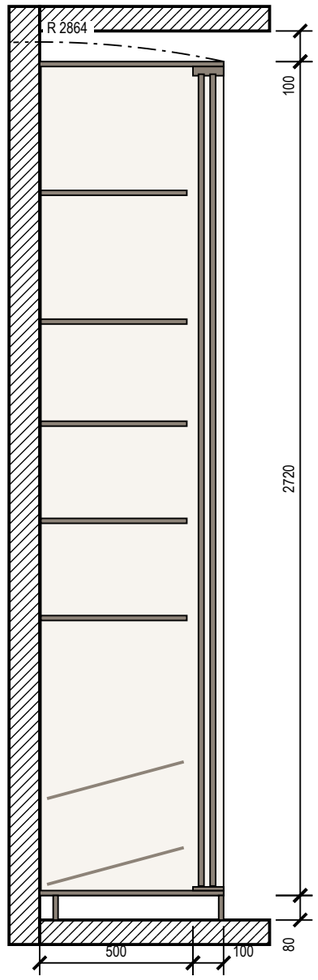

Примечания

1. Размеры — в мм по чистовой отделке; изделие 1400×600×2800 (Ш×Г×В). Перед раскроем — контрольный замер цеха после чистовой отделки стен, пола и потолка.
2. Корпус — ЛДСП 16 мм, задняя стенка ХДФ 4 мм в паз, цоколь 80 мм на регулируемых опорах; двери купе — ЛДСП 10 мм в алюминиевом профиле, нахлёст 30 мм, ширина двери 699 мм, высота — проём минус 40 мм; цвет — по колерной карте.
3. Кромка: скрытые торцы 0,4 мм, видимые 2 мм (ПВХ/АБС).
4. Номинальные зазоры: дверь купе — боковина 3 мм, фасад ящика — стойка 2 мм; ящики внутри купе — с накладкой 30 мм на стойке со стороны нахлёста дверей.
5. Ящики — направляющие полного выдвижения NL 450 (внутренняя глубина 496 мм ≥ NL + 3); присадка по 32-й системе — выполняет цех.
6. Зазор до потолка 100 мм — закрыть планкой в цвет корпуса при монтаже.
7. Подъём корпуса: диагональ боковины $\sqrt{(2800^2 + 600^2)}$ = 2864 мм < 2900 мм до потолка — корпус собирается лёжа и поднимается поворотом.
8. Крепление к стене от опрокидывания — уголки 2 шт. к несущему основанию (монтажная схема шкафов).

Условные обозначения

- дверь купе, стрелка — направление движения
- корпус и полки ЛДСП (вид на стену)
- задняя стенка ХДФ
- деталь в разрезе
- штанга для плечиков (на разрезе — плечики 450 мм)
- траектория угла корпуса при подъёме в проектное положение

Допущения и предложения на листе

Основа листа: взаимное расположение помещений, контур дома 9600 × 8000 и раскладка этажей подобраны проектировщиком под габариты помещений брифа; обмер и проект АР — задание (К-1); высота потолка 2900 мм — по брифу, не замерена; перекрытие 330 мм и отметка 2-го этажа +3,230 приняты; проект КР — задание (К-2); наружные стены 400 мм, перегородки 120 мм приняты (в брифе толщин нет) (К-1); разрешённая мощность 15 кВт принята по типовым ТУ для частного дома (К-4).
См. лист открытых вопросов (лист 6, записи К-1, К-2, К-4).

1000 мм · печать 1:1

Изм.	Кол.уч	Лист	№ док.	Подп.	Дата
Разраб.		Кырлан А.С.			19.10.26
Пров.					
ГИП					
Н. контр.					
Утв.					

ГД-2026-012-АИ

Дом 120 м²

Общая площадь 147,36* м² · * размеры приняты, не замерены (реестр — л. 6, К-1)

Дизайн-проект интерьера

Стадия	Лист	Листов
РП	76	130

Шкаф-купе Пр1

М 1:20

Кырлан Александр Сергеевич

выпуск 19.10.2026 № 53e4f7ddae · стр. 81 из 160

Шкаф распашной М4

Спальня родителей (пом. 6) · вид из помещения · размеры в мм, отметки в м

ПРЕДВАРИТЕЛЬНО · не для производства работ · открыто пунктов: 6 (реестр — л. 6)

Вид с фасадами

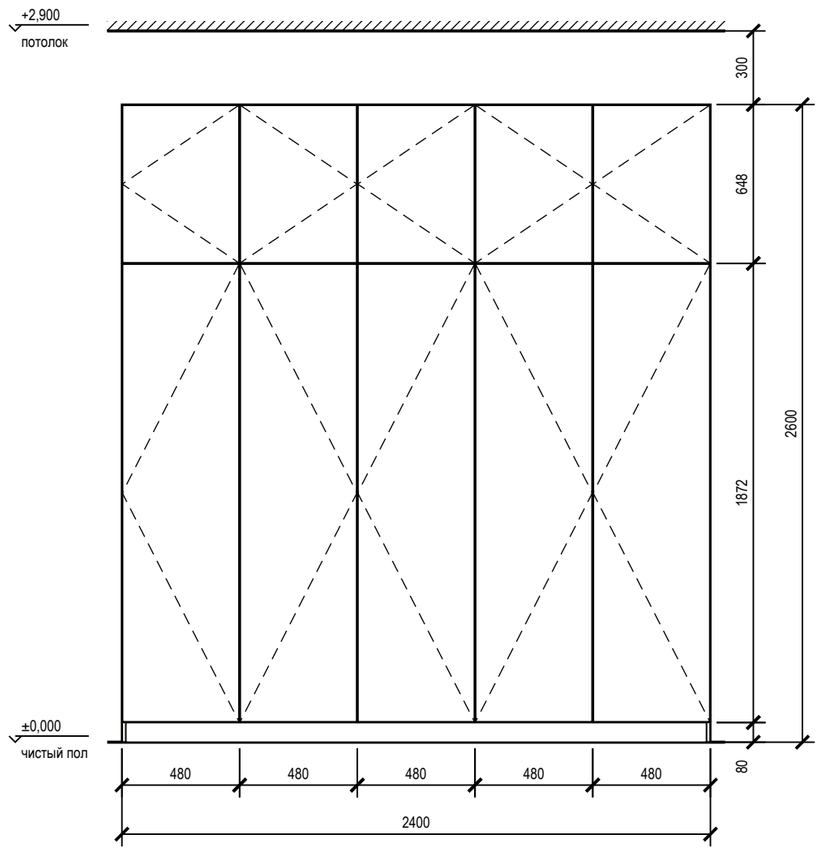

Вид без фасадов

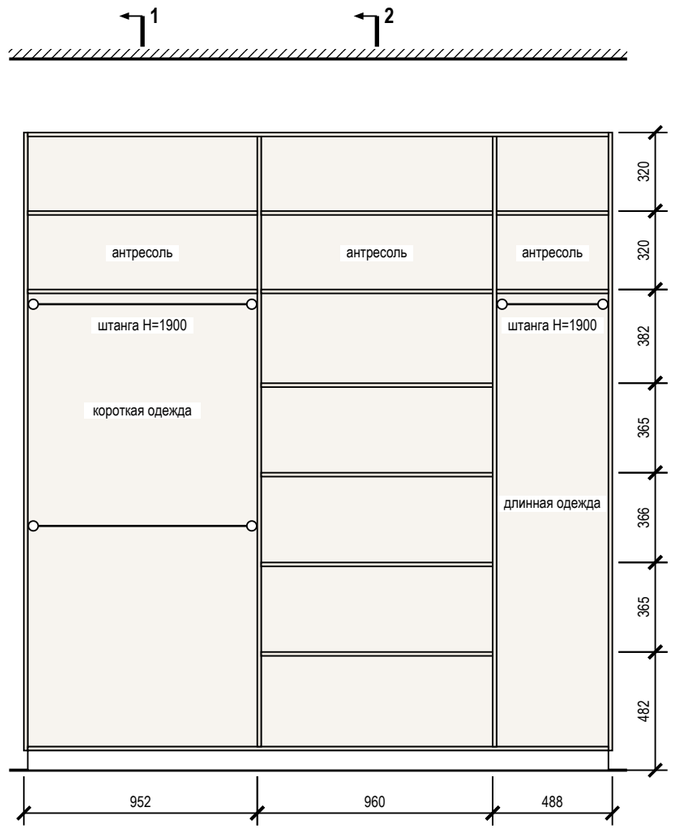

Разрез 1-1

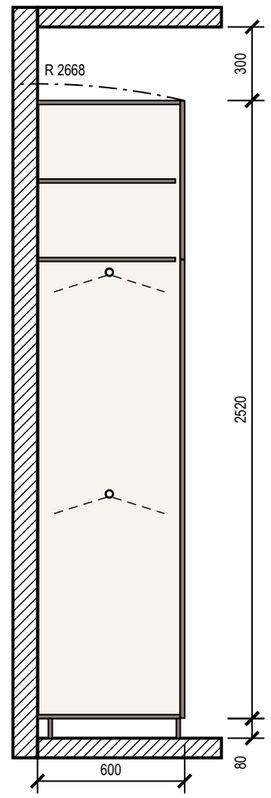

Разрез 2-2

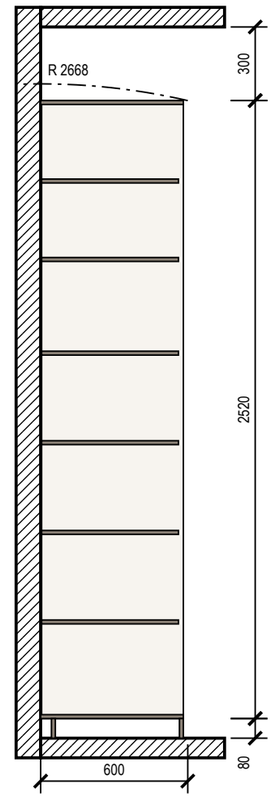

Примечания

1. Размеры — в мм по чистовой отделке; изделие 2400×600×2600 (Ш×Г×В). Перед раскроем — контрольный замер цеха после чистовой отделки стен, пола и потолка.
2. Корпус — ЛДСП 16 мм, задняя стенка ХДФ 4 мм в паз, цоколь 80 мм на регулируемых опорах; фасады — МДФ, эмаль матовая 18 мм накладные, цвет — по колерной карте; петли с доводчиком: фасад 1869 мм — 4 петли, фасад 645 мм — 2 петли.
3. Кромка: скрытые торцы 0,4 мм, видимые 2 мм (ПВХ/АБС).
4. Номинальные зазоры: между фасадами 3 мм, фасад — стена и фасад — потолок не менее 3 мм, фасад ящика — стойка 2 мм.
5. Ящики — направляющие полного выдвижения NL 550 (внутренняя глубина 578 мм ≥ NL + 3); присадка по 32-й системе — выполняет цех.
6. Зазор до потолка 300 мм.
7. Подъём корпуса: диагональ боковины √(2600² + 600²) = 2668 мм < 2900 мм до потолка — корпус собирается лёжа и поднимается поворотом.
8. Крепление к стене от опрокидывания — уголки 2 шт. к несущему основанию (монтажная схема шкафов).

Условные обозначения

- фасад распашной: линии сходятся к стороне петель
- корпус и полки ЛДСП (вид на стену)
- задняя стенка ХДФ
- деталь в разрезе
- штанга для плечиков (на разрезе — плечики 450 мм)
- траектория угла корпуса при подъёме в проектное положение

Допущения и предложения на листе

Основа листа: взаимное расположение помещений, контур дома 9600 × 8000 и раскладка этажей подобраны проектировщиком под габариты помещений брифа; обмер и проект АР — задание (К-1); высота потолка 2900 мм — по брифу, не замерена; перекрытие 330 мм и отметка 2-го этажа +3,230 приняты; проект КР — задание (К-2); наружные стены 400 мм, перегородки 120 мм приняты (в брифе толщин нет) (К-1); разрешённая мощность 15 кВт принята по типовым ТУ для частного дома (К-4).
См. лист открытых вопросов (лист 6, записи К-1, К-2, К-4).

1000 мм · печать 1:1

Изм.	Кол.уч	Лист	№ док.	Подп.	Дата
Разраб.		Кырлан А.С.			19.10.26
Пров.					
ГИП					
Н. контр.					
Утв.					

ГД-2026-012-АИ

Дом 120 м²

Общая площадь 147,36* м² · * размеры приняты, не замерены (реестр — л. 6, К-1)

Дизайн-проект интерьера	Стадия	Лист	Листов
	РП	77	130

Шкаф распашной М4

М 1:25

Кырлан Александр Сергеевич

выпуск 19.10.2026 № 53e4f7ddae · стр. 82 из 160

Шкаф распашной ДЗ

Детская (пом. 7) · вид из помещения · размеры в мм, отметки в м

ПРЕДВАРИТЕЛЬНО · не для производства работ · открыто пунктов: 6 (реестр — л. 6)

Вид с фасадами

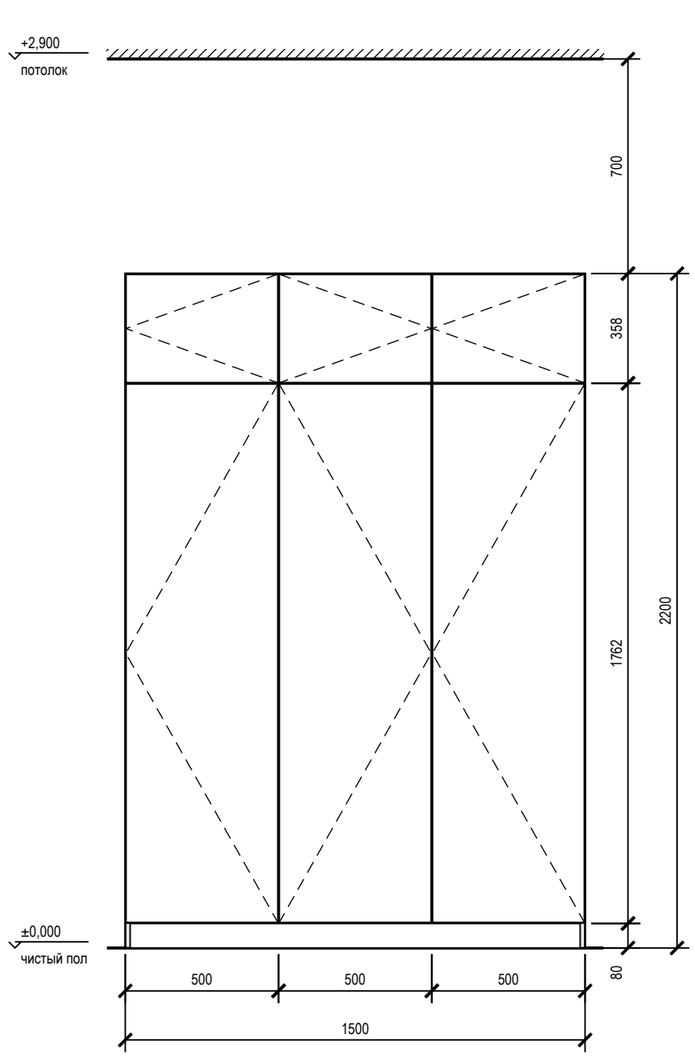

Вид без фасадов

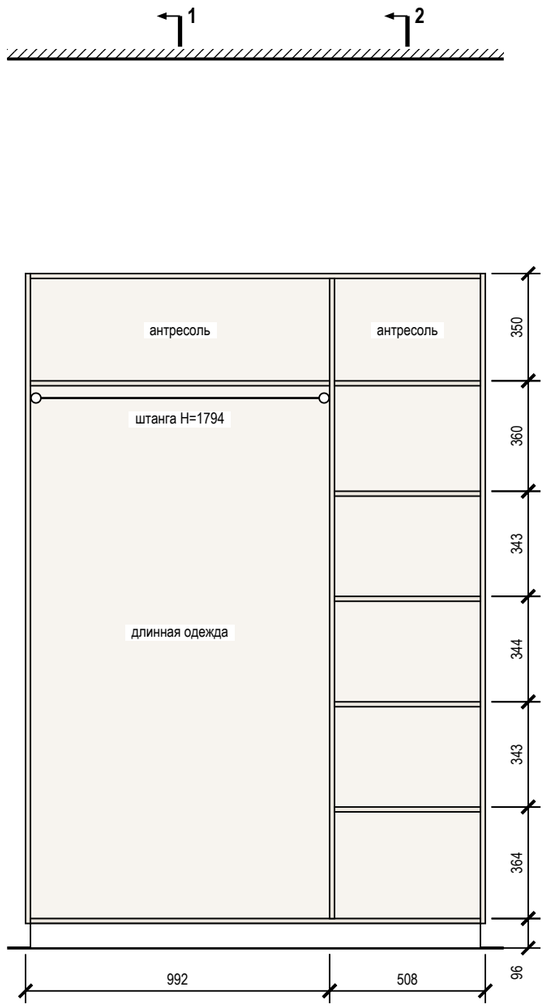

Разрез 1-1

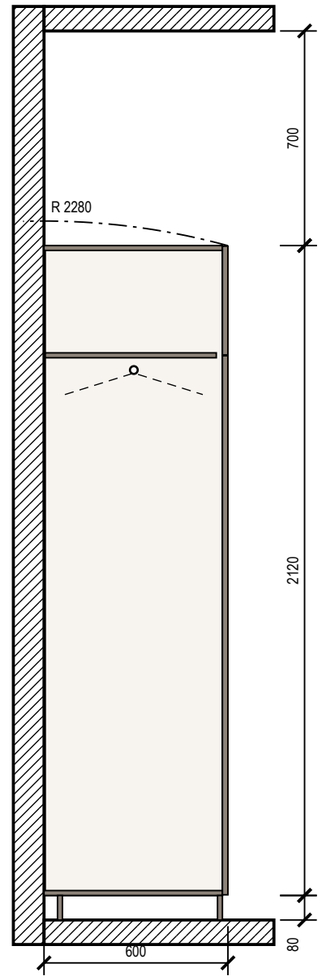

Разрез 2-2

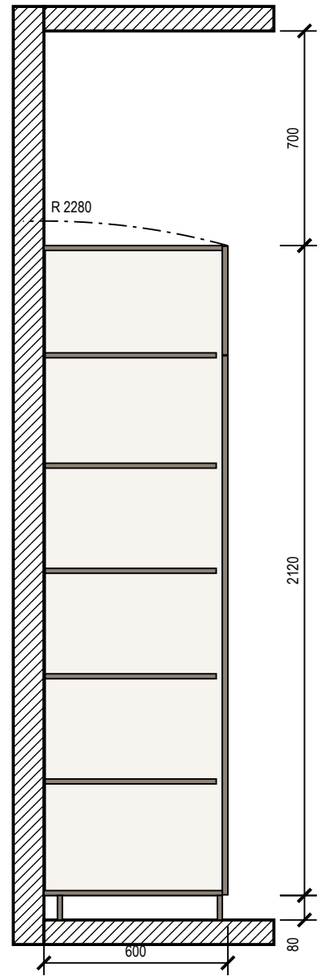

Примечания

1. Размеры — в мм по чистовой отделке; изделие 1500×600×2200 (Ш×Г×В). Перед раскроем — контрольный замер цеха после чистовой отделки стен, пола и потолка.
2. Корпус — ЛДСП 16 мм, задняя стенка ХДФ 4 мм в паз, цоколь 80 мм на регулируемых опорах; фасады — МДФ, эмаль матовая 18 мм накладные, цвет — по колерной карте; петли с доводчиком: фасад 1759 мм — 4 петли, фасад 355 мм — 2 петли.
3. Кромка: скрытые торцы 0,4 мм, видимые 2 мм (ПВХ/АБС).
4. Номинальные зазоры: между фасадами 3 мм, фасад — стена и фасад — потолок не менее 3 мм, фасад ящика — стойка 2 мм.
5. Ящики — направляющие полного выдвижения NL 550 (внутренняя глубина 578 мм ≥ NL + 3); присадка по 32-й системе — выполняет цех.
6. Зазор до потолка 700 мм.
7. Подъём корпуса: диагональ боковины $\sqrt{(2200^2 + 600^2)} = 2280$ мм < 2900 мм до потолка — корпус собирается лёжа и поднимается поворотом.
8. Крепление к стене от опрокидывания — уголки 2 шт. к несущему основанию (монтажная схема шкафов).

Условные обозначения

- фасад распашной: линии сходятся к стороне петель
- корпус и полки ЛДСП (вид на стену)
- задняя стенка ХДФ
- деталь в разрезе
- штанга для плечиков (на разрезе — плечики 450 мм)
- траектория угла корпуса при подъёме в проектное положение

Допущения и предложения на листе

Основа листа: взаимное расположение помещений, контур дома 9600 × 8000 и раскладка этажей подобраны проектировщиком под габариты помещений брифа; обмер и проект АР — задание (К-1); высота потолка 2900 мм — по брифу, не замерена; перекрытие 330 мм и отметка 2-го этажа +3,230 приняты; проект КР — задание (К-2); наружные стены 400 мм, перегородки 120 мм приняты (в брифе толщин нет) (К-1); разрешённая мощность 15 кВт принята по типовым ТУ для частного дома (К-4).
См. лист открытых вопросов (лист 6, записи К-1, К-2, К-4).

1000 мм · печать 1:1

Изм.	Кол.уч	Лист	№ док.	Подп.	Дата
Разраб.		Кырлан А.С.			19.10.26
Пров.					
ГИП					
Н. контр.					
Утв.					

ГД-2026-012-АИ

Дом 120 м²

Общая площадь 147,36* м² · * размеры приняты, не замерены (реестр — л. 6, К-1)

Дизайн-проект интерьера

Стадия	Лист	Листов
РП	78	130

Шкаф распашной ДЗ

М 1:20

Кырлан Александр Сергеевич

выпуск 19.10.2026 № 53e4f7ddae · стр. 83 из 160

Система хранения Гд1

Гардеробная (пом. 8) · вид из помещения · размеры в мм, отметки в м

ПРЕДВАРИТЕЛЬНО · не для производства работ · открыто пунктов: 6 (реестр — л. 6)

Общий вид

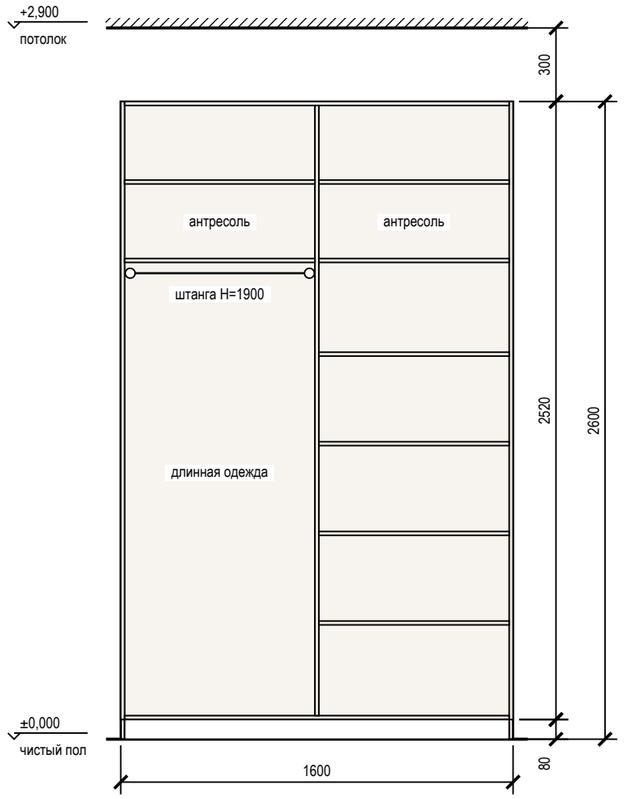

Наполнение, размеры в свету

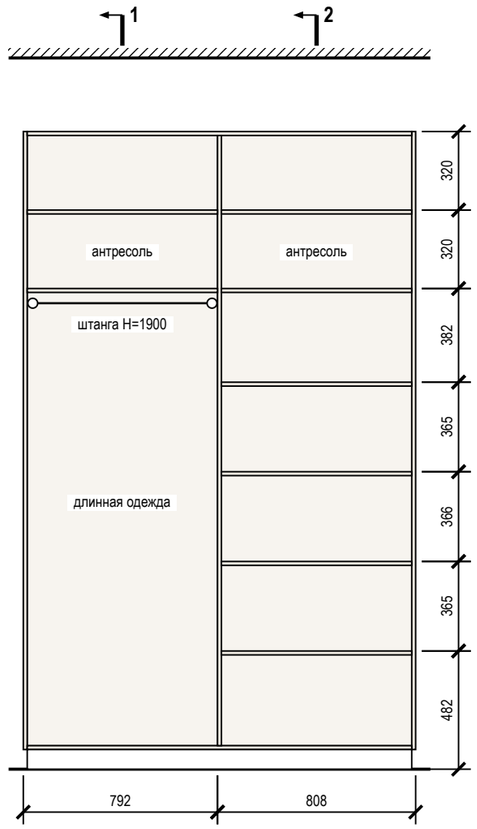

Разрез 1-1

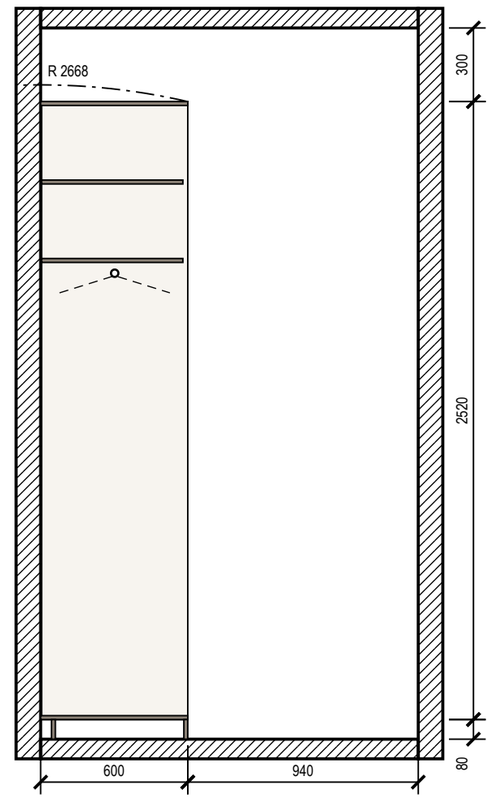

Разрез 2-2

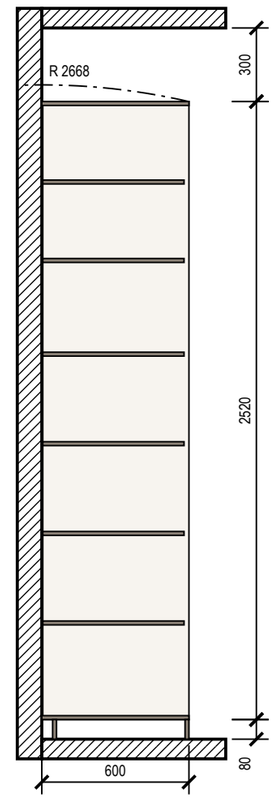

Примечания

1. Размеры — в мм по чистовой отделке; изделие 1600×600×2600 (Ш×Г×В). Перед раскроем — контрольный замер цеха после чистовой отделки стен, пола и потолка.
2. Корпус — ЛДСП 16 мм, задняя стенка ХДФ 4 мм в паз, цоколь 80 мм на регулируемых опорах; открытая система без фасадов, ящики с фасадами.
3. Кромка: скрытые торцы 0,4 мм, видимые 2 мм (ПВХ/АБС).
4. Номинальные зазоры: между фасадами ящиков 3 мм, фасад ящика — стойка 2 мм.
5. Ящики — направляющие полного выдвижения NL 550 (внутренняя глубина 596 мм ≥ NL + 3); присадка по 32-й системе — выполняет цех.
6. Зазор до потолка 300 мм.
7. Подъём корпуса: диагональ боковины $\sqrt{(2600^2 + 600^2)} = 2668$ мм < 2900 мм до потолка — корпус собирается лёжа и поднимается поворотом.
8. Крепление к стене от опрокидывания: true; основание стены и шаг анкеров — монтажная схема шкафов.
9. Проход перед изделием 940 мм показан на разрезе 1-1.

Условные обозначения

- корпус и полки ЛДСП (вид на стену)
- задняя стенка ХДФ
- деталь в разрезе
- штанга для плечиков (на разрезе — плечики 450 мм)
- траектория угла корпуса при подъёме в проектное положение

Допущения и предложения на листе

Основа листа: взаимное расположение помещений, контур дома 9600 × 8000 и раскладка этажей подобраны проектировщиком под габариты помещений брифа; обмер и проект АР — задание (К-1); высота потолка 2900 мм — по брифу, не замерена; перекрытие 330 мм и отметка 2-го этажа +3,230 приняты; проект КР — задание (К-2); наружные стены 400 мм, перегородки 120 мм приняты (в брифе толщин нет) (К-1); разрешённая мощность 15 кВт принята по типовым ТУ для частного дома (К-4).
См. лист открытых вопросов (лист 6, записи К-1, К-2, К-4).

1000 мм · печать 1:1

Изм.	Кол.уч	Лист	№ док.	Подп.	Дата
Разраб.		Кырлан А.С.			19.10.26
Пров.					
ГИП					
Н. контр.					
Утв.					

ГД-2026-012-АИ

Дом 120 м²

Общая площадь 147,36* м² · * размеры приняты, не замерены (реестр — л. 6, К-1)

Дизайн-проект интерьера

Стадия	Лист	Листов
РП	79	130

Система хранения Гд1

М 1:25

Кырлан Александр Сергеевич

выпуск 19.10.2026 № 53e4f7ddae · стр. 84 из 160

Система хранения Гд2

Гардеробная (пом. 8) · вид из помещения · размеры в мм, отметки в м

ПРЕДВАРИТЕЛЬНО · не для производства работ · открыто пунктов: 6 (реестр — л. 6)

Общий вид

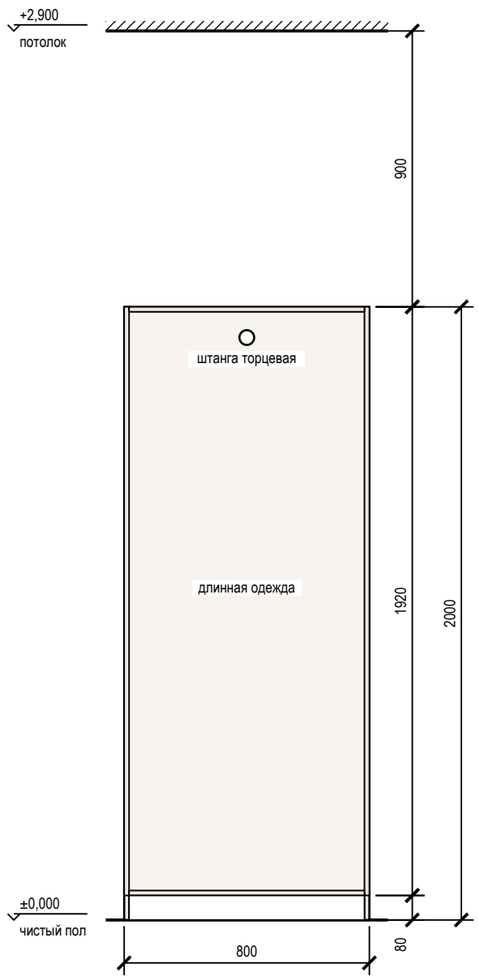

Наполнение, размеры в свету

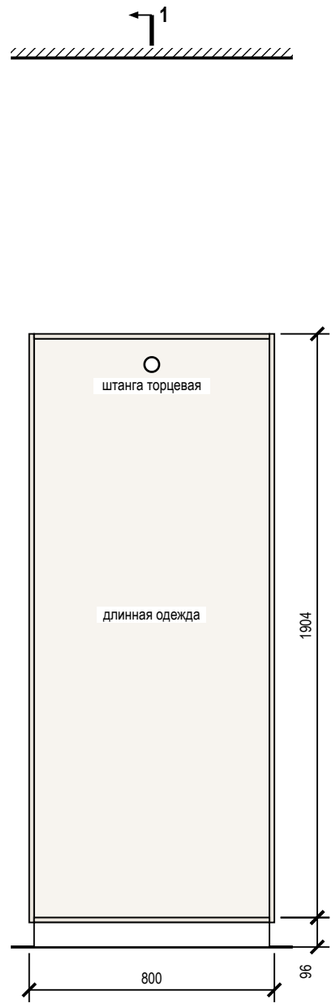

Разрез 1-1

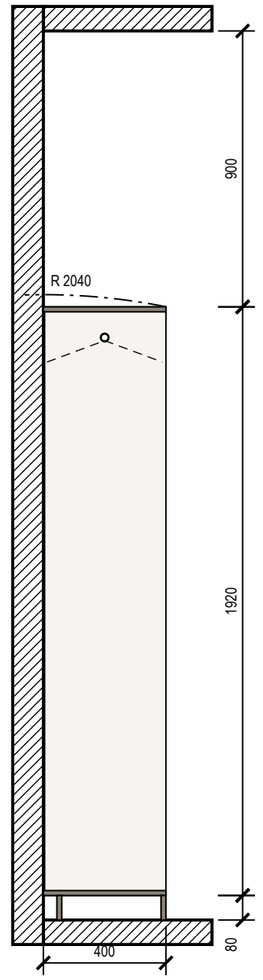

Примечания

1. Размеры — в мм по чистовой отделке; изделие 800×400×2000 (Ш×Г×В). Перед раскроем — контрольный замер цеха после чистовой отделки стен, пола и потолка.
2. Корпус — ЛДСП 16 мм, задняя стенка ХДФ 4 мм в паз, цоколь 80 мм на регулируемых опорах; открытая система без фасадов, ящики с фасадами.
3. Кромка: скрытые торцы 0,4 мм, видимые 2 мм (ПВХ/АБС).
4. Номинальные зазоры: между фасадами ящиков 3 мм, фасад ящика — стойка 2 мм.
5. Ящики — направляющие полного выдвижения NL 350 (внутренняя глубина 396 мм ≥ NL + 3); присадка по 32-й системе — выполняет цех.
6. Зазор до потолка 900 мм.
7. Подъём корпуса: диагональ боковины $\sqrt{(2000^2 + 400^2)} = 2040$ мм < 2900 мм до потолка — корпус собирается лёжа и поднимается поворотом.
8. Крепление к стене от опрокидывания: true; основание стены и шаг анкеров — монтажная схема шкафов.

Условные обозначения

- корпус и полки ЛДСП (вид на стену)
- задняя стенка ХДФ
- деталь в разрезе
- штанга для плечиков (на разрезе — плечики 450 мм)
- траектория угла корпуса при подъёме в проектное положение

Допущения и предложения на листе

Основа листа: взаимное расположение помещений, контур дома 9600 × 8000 и раскладка этажей подобраны проектировщиком под габариты помещений брифа; обмер и проект АР — задание (К-1); высота потолка 2900 мм — по брифу, не замерена; перекрытие 330 мм и отметка 2-го этажа +3,230 приняты; проект КР — задание (К-2); наружные стены 400 мм, перегородки 120 мм приняты (в брифе толщин нет) (К-1); разрешённая мощность 15 кВт принята по типовым ТУ для частного дома (К-4).
См. лист открытых вопросов (лист 6, записи К-1, К-2, К-4).

1000 мм · печать 1:1

Изм.	Кол.уч	Лист	№ док.	Подп.	Дата
Разраб.		Кырлан А.С.			19.10.26
Пров.					
ГИП					
Н. контр.					
Утв.					

ГД-2026-012-АИ

Дом 120 м²

Общая площадь 147,36* м² · * размеры приняты, не замерены (реестр — л. 6, К-1)

Дизайн-проект интерьера

Стадия	Лист	Листов
РП	80	130

Система хранения Гд2

М 1:20

Кырлан Александр Сергеевич

выпуск 19.10.2026 № 53e4f7ddae · стр. 85 из 160

Система хранения Кл1

Кладовая (пом. 9) · вид из помещения · размеры в мм, отметки в м

ПРЕДВАРИТЕЛЬНО · не для производства работ · открыто пунктов: 6 (реестр — л. 6)

Общий вид

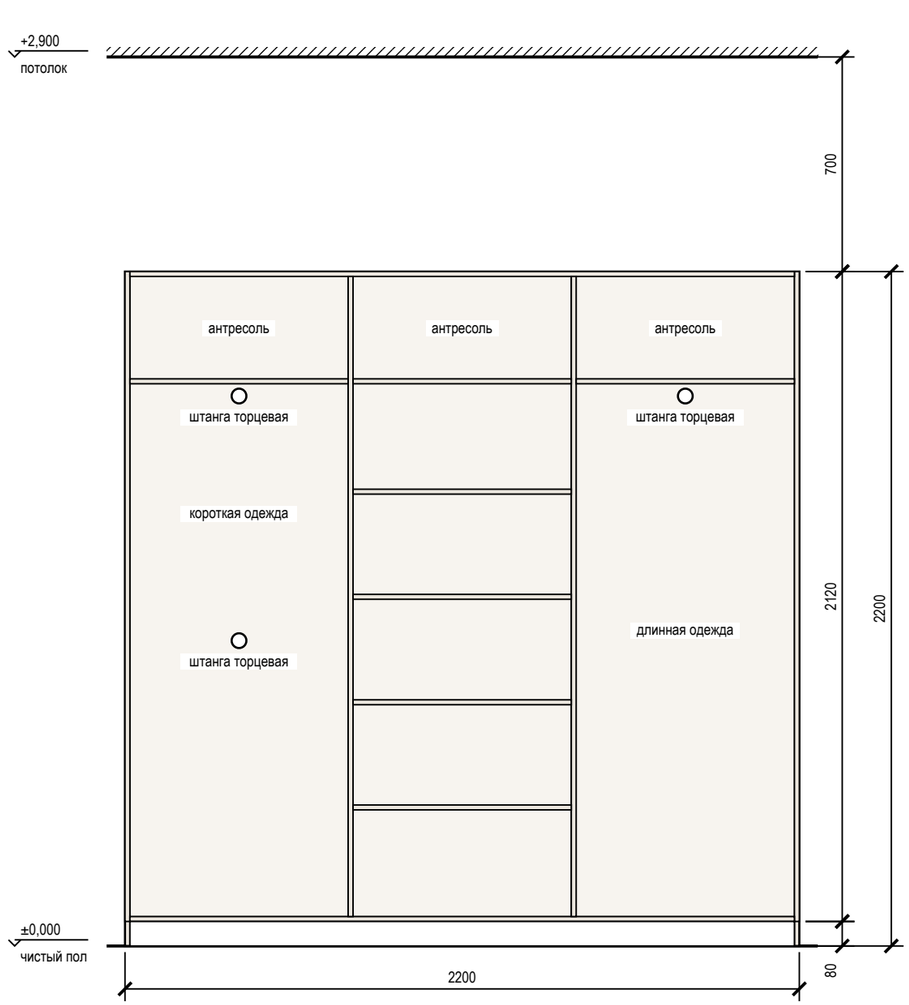

Наполнение, размеры в свету

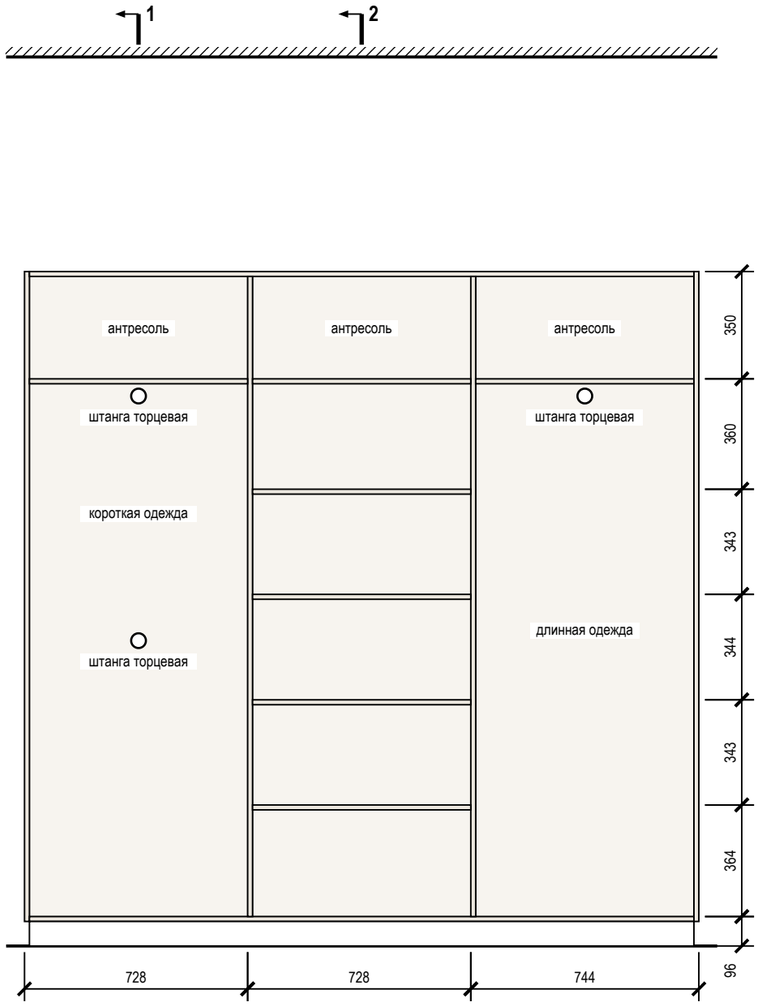

Разрез 1-1

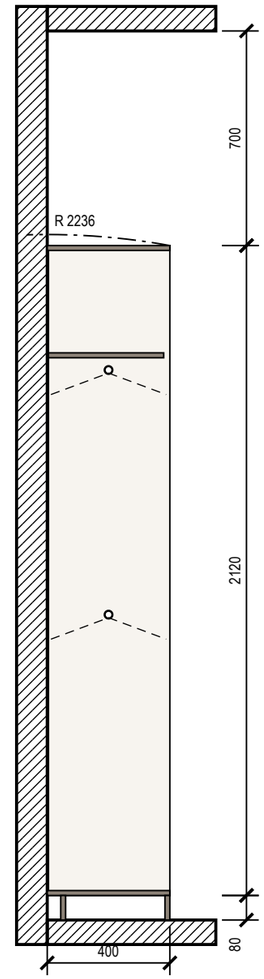

Разрез 2-2

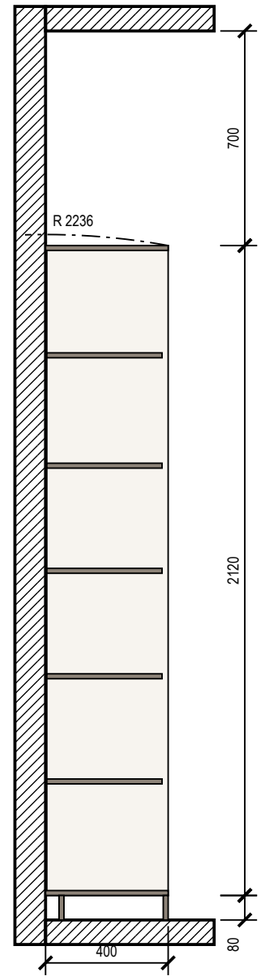

Примечания

1. Размеры — в мм по чистовой отделке; изделие 2200×400×2200 (Ш×Г×В). Перед раскроем — контрольный замер цеха после чистовой отделки стен, пола и потолка.
2. Корпус — ЛДСП 16 мм, задняя стенка ХДФ 4 мм в паз, цоколь 80 мм на регулируемых опорах; открытая система без фасадов, ящики с фасадами.
3. Кромка: скрытые торцы 0,4 мм, видимые 2 мм (ПВХ/АБС).
4. Номинальные зазоры: между фасадами ящиков 3 мм, фасад ящика — стойка 2 мм.
5. Ящики — направляющие полного выдвижения NL 350 (внутренняя глубина 396 мм ≥ NL + 3); присадка по 32-й системе — выполняет цех.
6. Зазор до потолка 700 мм.
7. Подъём корпуса: диагональ боковины √(2200² + 400²) = 2236 мм < 2900 мм до потолка — корпус собирается лёжа и поднимается поворотом.
8. Крепление к стене от опрокидывания: true; основание стены и шаг анкеров — монтажная схема шкафов.

Условные обозначения

- корпус и полки ЛДСП (вид на стену)
- задняя стенка ХДФ
- деталь в разрезе
- штанга для плечиков (на разрезе — плечики 450 мм)
- траектория угла корпуса при подъёме в проектное положение

Допущения и предложения на листе

Основа листа: взаимное расположение помещений, контур дома 9600 × 8000 и раскладка этажей подобраны проектировщиком под габариты помещений брифа; обмер и проект АР — задание (К-1); высота потолка 2900 мм — по брифу, не замерена; перекрытие 330 мм и отметка 2-го этажа +3,230 приняты; проект КР — задание (К-2); наружные стены 400 мм, перегородки 120 мм приняты (в брифе толщин нет) (К-1); разрешённая мощность 15 кВт принята по типовым ТУ для частного дома (К-4).

См. лист открытых вопросов (лист 6, записи К-1, К-2, К-4).

1000 мм · печать 1:1

Изм.	Кол.уч	Лист	№ док.	Подп.	Дата
Разраб.		Кырлан А.С.			19.10.26
Пров.					
ГИП					
Н. контр.					
Утв.					

ГД-2026-012-АИ

Дом 120 м²

Общая площадь 147,36* м² · * размеры приняты, не замерены (реестр — л. 6, К-1)

Дизайн-проект интерьера

Стадия	Лист	Листов
РП	81	130

Система хранения Кл1

М 1:20

Кырлан Александр Сергеевич

выпуск 19.10.2026 № 53e4f7ddae · стр. 86 из 160

Система хранения Кл2

Кладовая (пом. 9) · вид из помещения · размеры в мм, отметки в м

ПРЕДВАРИТЕЛЬНО · не для производства работ · открыто пунктов: 6 (реестр — л. 6)

Общий вид

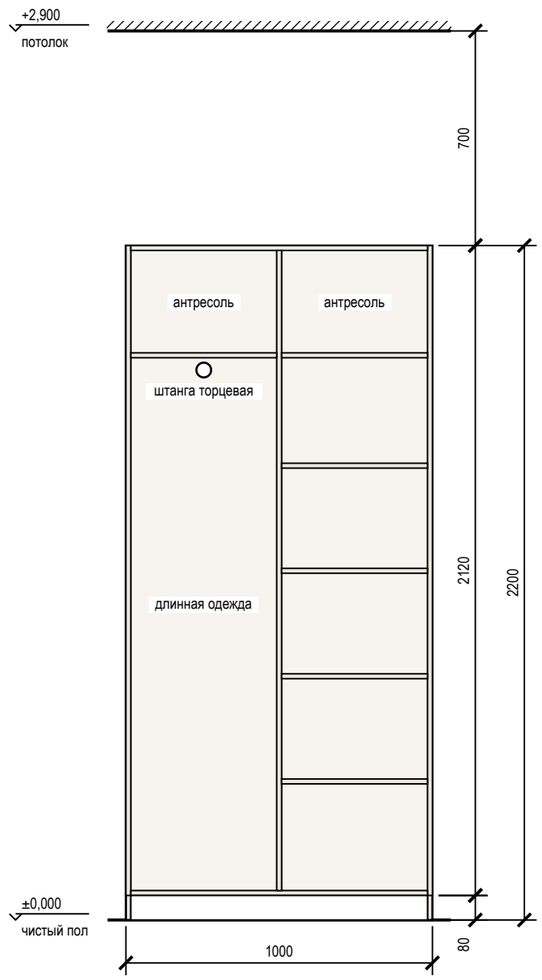

Наполнение, размеры в свету

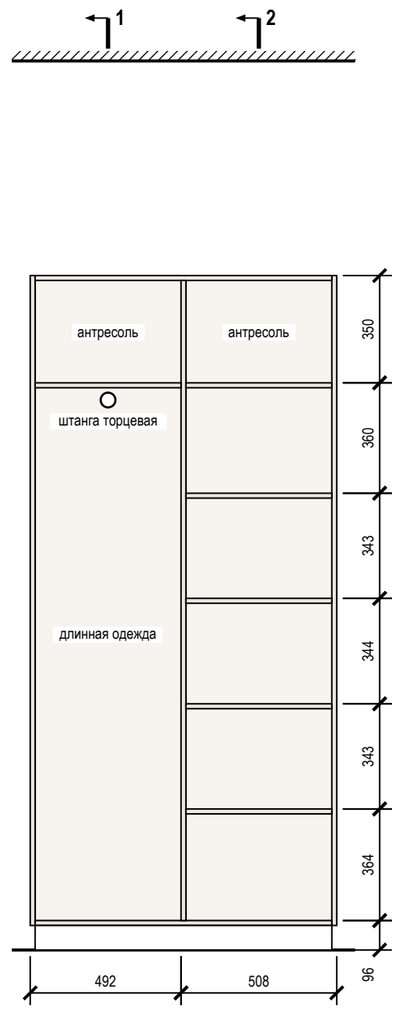

Разрез 1-1

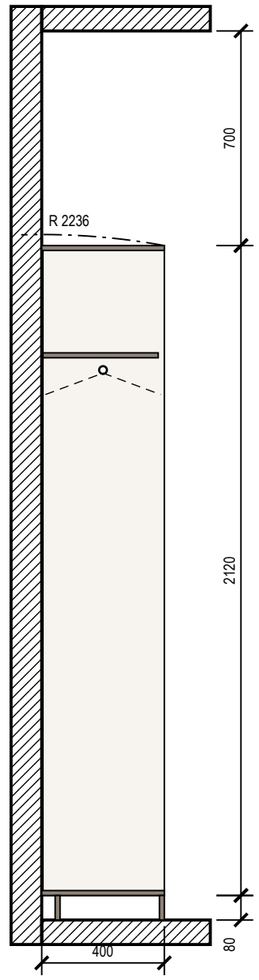

Разрез 2-2

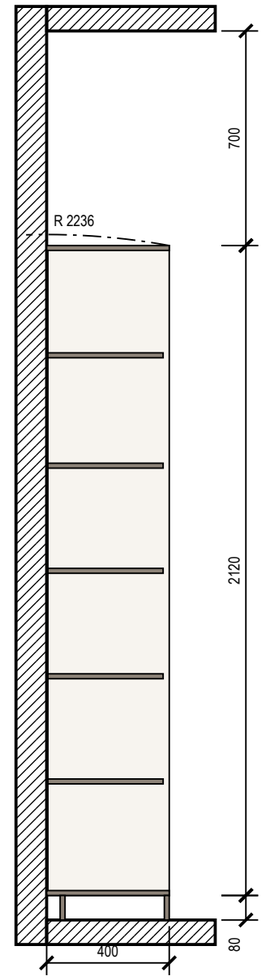

Примечания

1. Размеры — в мм по чистовой отделке; изделие 1000×400×2200 (Ш×Г×В). Перед раскроем — контрольный замер цеха после чистовой отделки стен, пола и потолка.
2. Корпус — ЛДСП 16 мм, задняя стенка ХДФ 4 мм в паз, цоколь 80 мм на регулируемых опорах; открытая система без фасадов, ящики с фасадами.
3. Кромка: скрытые торцы 0,4 мм, видимые 2 мм (ПВХ/АБС).
4. Номинальные зазоры: между фасадами ящиков 3 мм, фасад ящика — стойка 2 мм.
5. Ящики — направляющие полного выдвижения NL 350 (внутренняя глубина 396 мм ≥ NL + 3); присадка по 32-й системе — выполняет цех.
6. Зазор до потолка 700 мм.
7. Подъём корпуса: диагональ боковины √(2200² + 400²) = 2236 мм < 2900 мм до потолка — корпус собирается лёжа и поднимается поворотом.
8. Крепление к стене от опрокидывания: true; основание стены и шаг анкеров — монтажная схема шкафов.

Условные обозначения

- корпус и полки ЛДСП (вид на стену)
- задняя стенка ХДФ
- деталь в разрезе
- штанга для плечиков (на разрезе — плечики 450 мм)
- траектория угла корпуса при подъёме в проектное положение

Допущения и предложения на листе

Основа листа: взаимное расположение помещений, контур дома 9600 × 8000 и раскладка этажей подобраны проектировщиком под габариты помещений брифа; обмер и проект АР — задание (К-1); высота потолка 2900 мм — по брифу, не замерена; перекрытие 330 мм и отметка 2-го этажа +3,230 приняты; проект КР — задание (К-2); наружные стены 400 мм, перегородки 120 мм приняты (в брифе толщин нет) (К-1); разрешённая мощность 15 кВт принята по типовым ТУ для частного дома (К-4).
См. лист открытых вопросов (лист 6, записи К-1, К-2, К-4).

1000 мм · печать 1:1

Изм.	Кол.уч	Лист	№ док.	Подп.	Дата
Разраб.		Кырлан А.С.			19.10.26
Пров.					
ГИП					
Н. контр.					
Утв.					

ГД-2026-012-АИ

Дом 120 м²

Общая площадь 147,36* м² · * размеры приняты, не замерены (реестр — л. 6, К-1)

Дизайн-проект интерьера

Стадия	Лист	Листов
РП	82	130

Система хранения Кл2

М 1:20

Кырлан Александр Сергеевич

выпуск 19.10.2026 № 53e4f7ddae · стр. 87 из 160

Шкаф распашной Д8

Детская вторая (пом. 12) · вид из помещения · размеры в мм, отметки в м

ПРЕДВАРИТЕЛЬНО · не для производства работ · открыто пунктов: 6 (реестр — л. 6)

Вид с фасадами

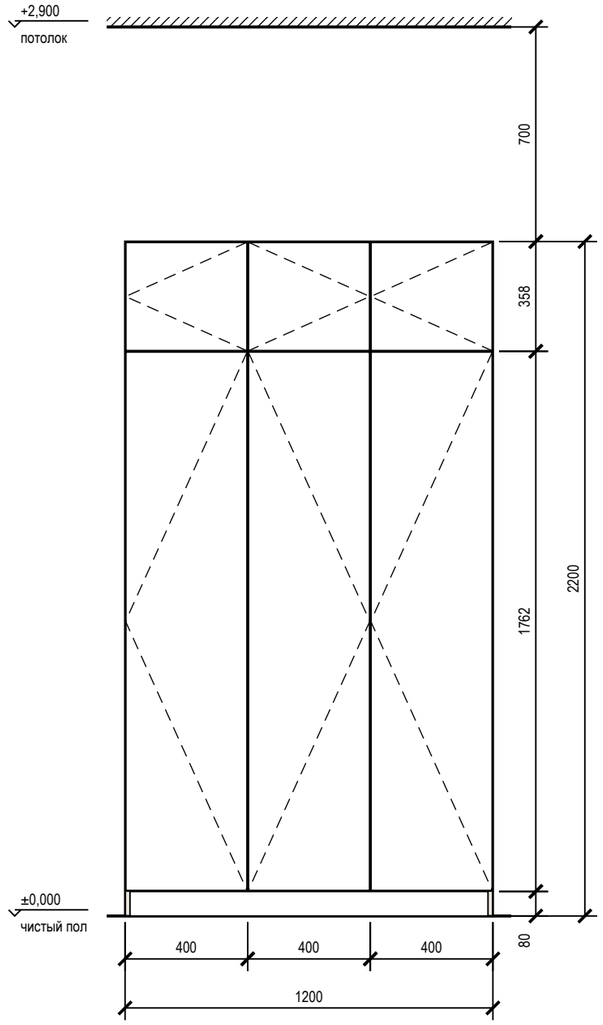

Вид без фасадов

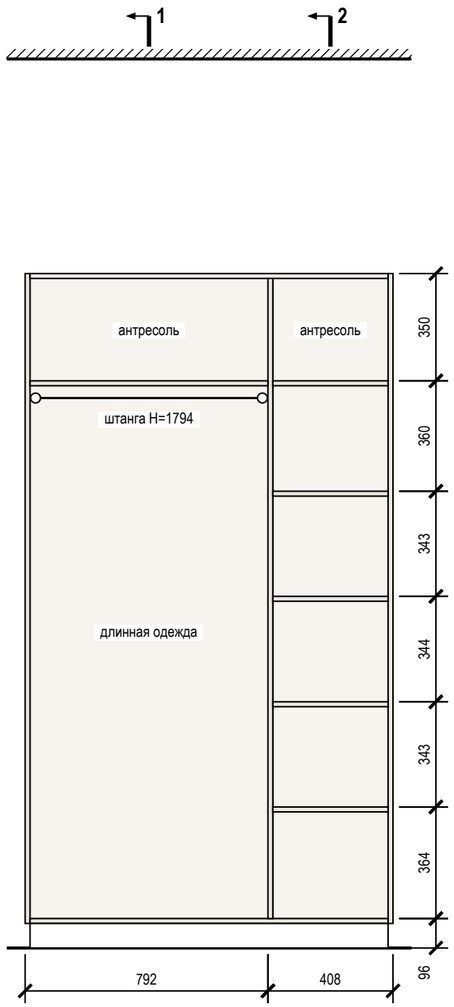

Разрез 1-1

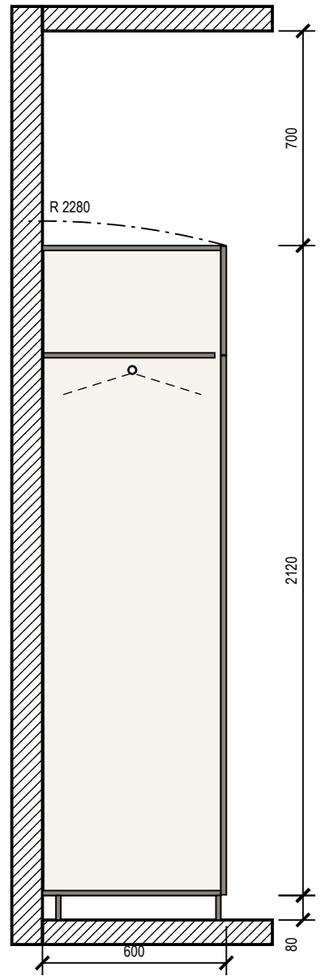

Разрез 2-2

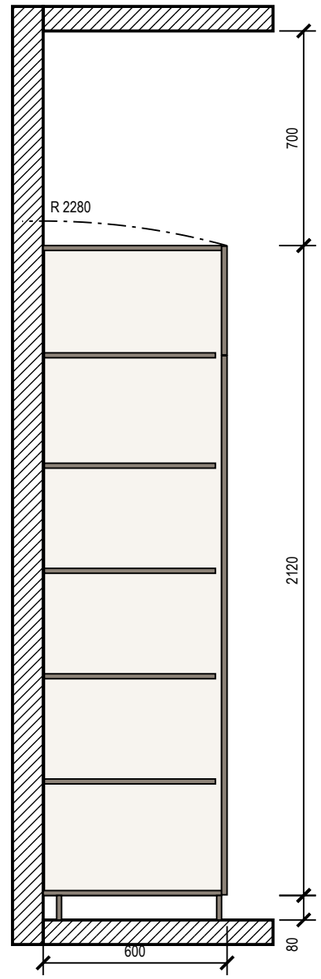

Примечания

1. Размеры — в мм по чистовой отделке; изделие 1200×600×2200 (Ш×Г×В). Перед раскроем — контрольный замер цеха после чистовой отделки стен, пола и потолка.
2. Корпус — ЛДСП 16 мм, задняя стенка ХДФ 4 мм в паз, цоколь 80 мм на регулируемых опорах; фасады — МДФ, эмаль матовая 18 мм накладные, цвет — по колерной карте; петли с доводчиком: фасад 1759 мм — 4 петли, фасад 355 мм — 2 петли.
3. Кромка: скрытые торцы 0,4 мм, видимые 2 мм (ПВХ/АБС).
4. Номинальные зазоры: между фасадами 3 мм, фасад — стена и фасад — потолок не менее 3 мм, фасад ящика — стойка 2 мм.
5. Ящики — направляющие полного выдвижения NL 550 (внутренняя глубина 578 мм ≥ NL + 3); присадка по 32-й системе — выполняет цех.
6. Зазор до потолка 700 мм.
7. Подъём корпуса: диагональ боковины $\sqrt{(2200^2 + 600^2)} = 2280$ мм < 2900 мм до потолка — корпус собирается лёжа и поднимается поворотом.
8. Крепление к стене от опрокидывания — уголки 2 шт. к несущему основанию (монтажная схема шкафов).

Условные обозначения

- фасад распашной: линии сходятся к стороне петель
- корпус и полки ЛДСП (вид на стену)
- задняя стенка ХДФ
- деталь в разрезе
- штанга для плечиков (на разрезе — плечики 450 мм)
- траектория угла корпуса при подъёме в проектное положение

Допущения и предложения на листе

Основа листа: взаимное расположение помещений, контур дома 9600 × 8000 и раскладка этажей подобраны проектировщиком под габариты помещений брифа; обмер и проект АР — задание (К-1); высота потолка 2900 мм — по брифу, не замерена; перекрытие 330 мм и отметка 2-го этажа +3,230 приняты; проект КР — задание (К-2); наружные стены 400 мм, перегородки 120 мм приняты (в брифе толщин нет) (К-1); разрешённая мощность 15 кВт принята по типовым ТУ для частного дома (К-4).
См. лист открытых вопросов (лист 6, записи К-1, К-2, К-4).

1000 мм · печать 1:1

Изм.	Кол.уч	Лист	№ док.	Подп.	Дата
Разраб.		Кырлан А.С.			19.10.26
Пров.					
ГИП					
Н. контр.					
Утв.					

ГД-2026-012-АИ

Дом 120 м²

Общая площадь 147,36* м² · * размеры приняты, не замерены (реестр — л. 6, К-1)

Дизайн-проект интерьера	Стадия	Лист	Листов
	РП	83	130

Шкаф распашной Д8

М 1:20

Кырлан Александр Сергеевич

выпуск 19.10.2026 № 53e4f7ddae · стр. 88 из 160

Система хранения Д10

Детская вторая (пом. 12) · вид из помещения · размеры в мм, отметки в м

ПРЕДВАРИТЕЛЬНО · не для производства работ · открыто пунктов: 6 (реестр — л. 6)

Общий вид

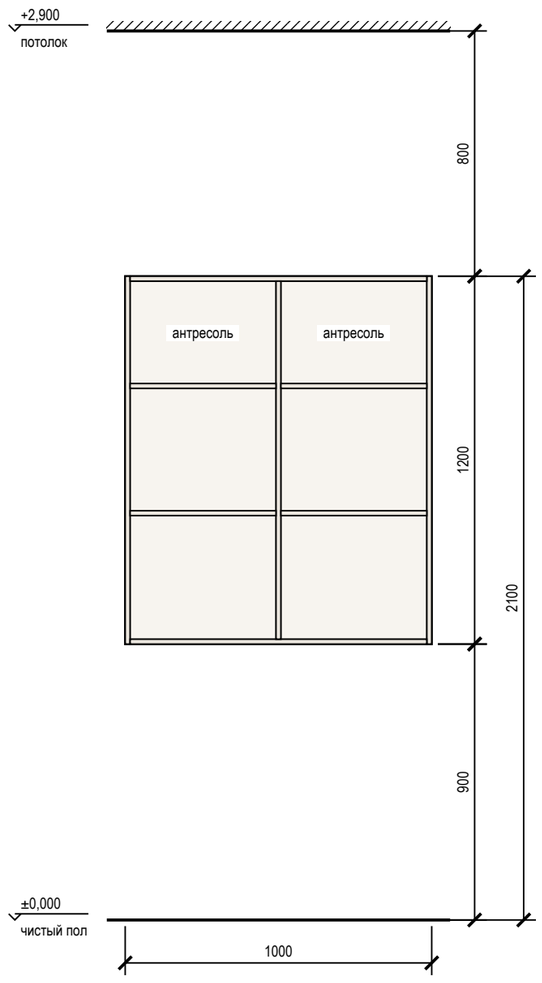

Наполнение, размеры в свету

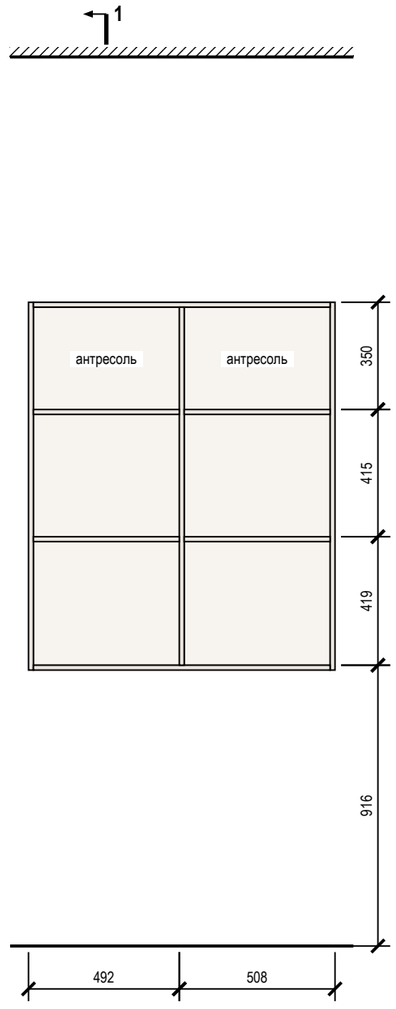

Разрез 1-1

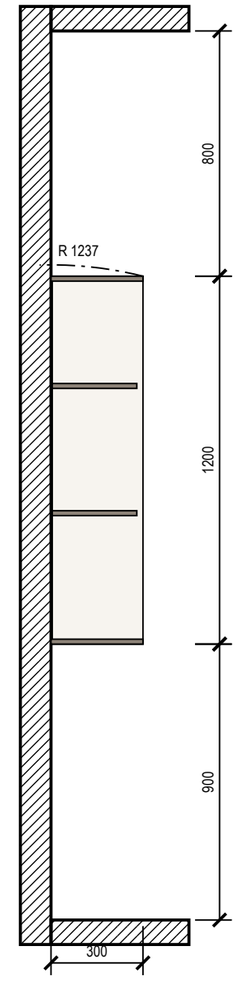

Примечания

1. Размеры — в мм по чистовой отделке; изделие 1000×300×1200 (Ш×Г×В). Перед раскроем — контрольный замер цеха после чистовой отделки стен, пола и потолка.
2. Корпус — ЛДСП 16 мм, задняя стенка ХДФ 4 мм в паз, цоколь 0 мм на регулируемых опорах; открытая система без фасадов, ящики с фасадами.
3. Кромка: скрытые торцы 0,4 мм, видимые 2 мм (ПВХ/АБС).
4. Номинальные зазоры: между фасадами ящиков 3 мм, фасад ящика — стойка 2 мм.
5. Ящики — направляющие полного выдвижения NL 270 (внутренняя глубина 296 мм ≥ NL + 3); присадка по 32-й системе — выполняет цех.
6. Зазор до потолка 800 мм.
7. Подъём корпуса: диагональ боковины $\sqrt{(1200^2 + 300^2)} = 1237$ мм < 2000 мм до потолка — корпус собирается лёжа и поднимается поворотом.
8. Крепление к стене от опрокидывания: true; основание стены и шаг анкеров — монтажная схема шкафов.

Условные обозначения

- корпус и полки ЛДСП (вид на стену)
- задняя стенка ХДФ
- деталь в разрезе
- штанга для плечиков (на разрезе — плечики 450 мм)
- траектория угла корпуса при подъёме в проектное положение

Допущения и предложения на листе

Основа листа: взаимное расположение помещений, контур дома 9600 × 8000 и раскладка этажей подобраны проектировщиком под габариты помещений брифа; обмер и проект АР — задание (К-1); высота потолка 2900 мм — по брифу, не замерена; перекрытие 330 мм и отметка 2-го этажа +3,230 приняты; проект КР — задание (К-2); наружные стены 400 мм, перегородки 120 мм приняты (в брифе толщин нет) (К-1); разрешённая мощность 15 кВт принята по типовым ТУ для частного дома (К-4).
См. лист открытых вопросов (лист 6, записи К-1, К-2, К-4).

1000 мм · печать 1:1

Изм.	Кол.уч	Лист	№ док.	Подп.	Дата
Разраб.		Кырлан А.С.			19.10.26
Пров.					
ГИП					
Н. контр.					
Утв.					

ГД-2026-012-АИ

Дом 120 м²

Общая площадь 147,36* м² · * размеры приняты, не замерены (реестр — л. 6, К-1)

Дизайн-проект интерьера

Стадия	Лист	Листов
РП	84	130

Система хранения Д10

М 1:20

Кырлан Александр Сергеевич

выпуск 19.10.2026 № 53e4f7ddae · стр. 89 из 160

Кухня (пом. 1). Развёртка гарнитура

Гостиная-кухня (пом. 1) · стена А · вид из помещения · размеры в мм, отметки в м

ПРЕДВАРИТЕЛЬНО · не для производства работ · открыто пунктов: 6 (реестр — л. 6)

Вид с фасадами

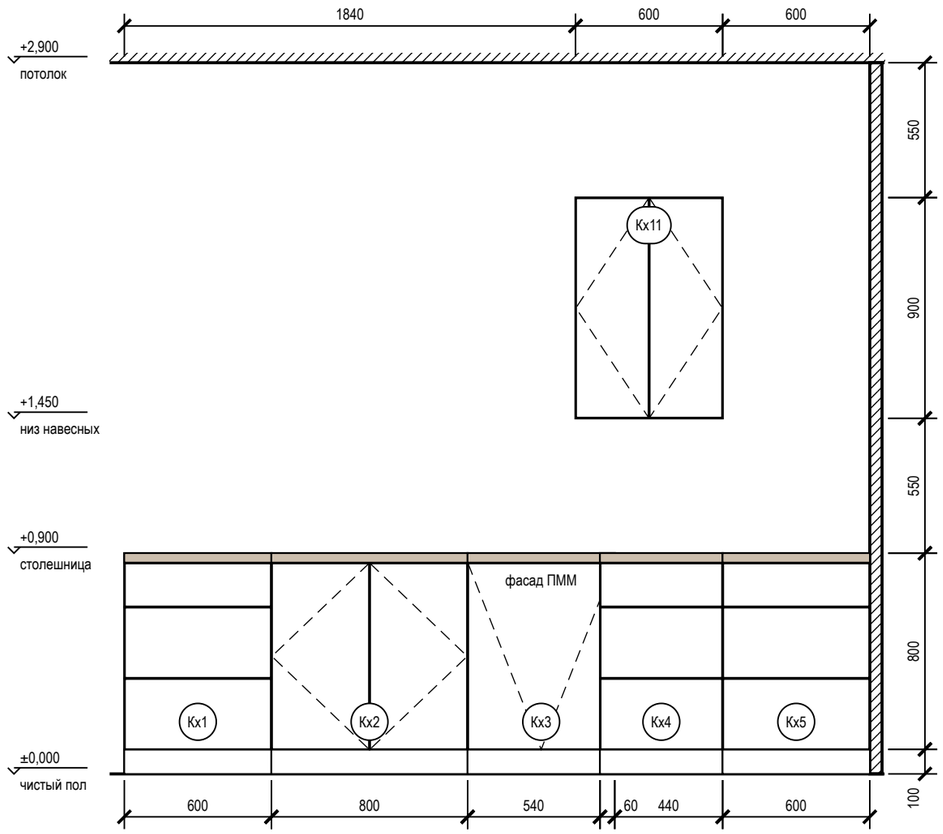

Вид без фасадов (наполнение, выводы)

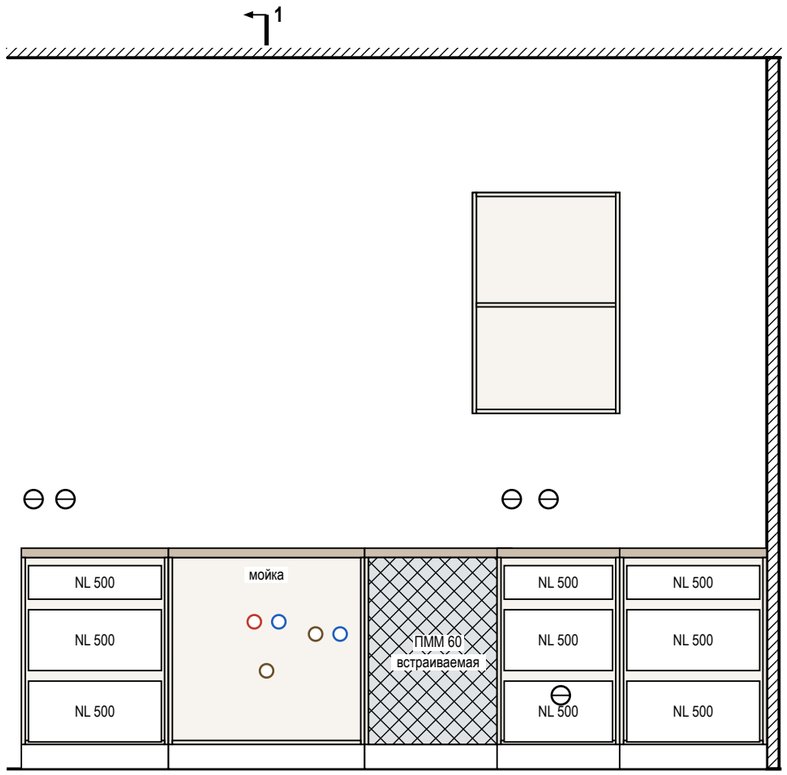

Разрез 1-1

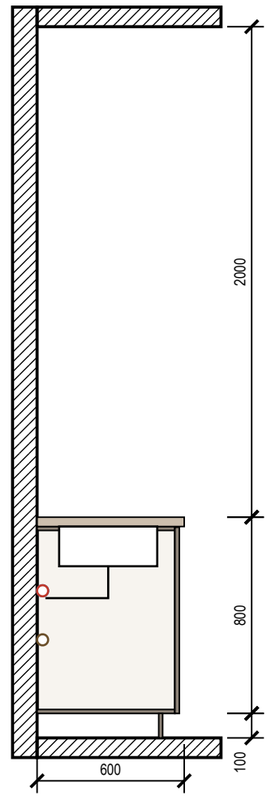

Условные обозначения

- фасад распашной: линии сходятся к стороне петель
- фасад ящика, карго
- встраиваемая техника
- столешница
- доборная планка
- деталь в разрезе
- К1 — марка модуля
- розетка на стене
- вывод кабеля к технике
- В1 — вывод воды В1 / Т3, канализации К1

Примечания

1. Размеры — в мм по чистовой отделке, вид из помещения; марки — как на плане расстановки. Перед раскроем — контрольный замер цеха после фартука и пола.
2. Корпуса — ЛДСП 16 мм, задняя стенка ХДФ 4 мм; фасады — МДФ, эмаль матовая 18 мм, цвет по колерной карте; столешница 38 мм, свес 20 мм; цоколь 100 мм.
3. Кромка: скрытые торцы 0,4 мм, видимые 2 мм. Номинальные зазоры: между фасадами 3 мм, фасад — столешница 3 мм, фасад — стена не менее 3 мм.
4. Ящики полного выдвижения и петли — с доводчиком; присадка по 32-й системе — выполняет цех.
5. Ниши техники — по монтажным схемам выбранных моделей: решётка в цоколе и канал за пеналом холодильника, зазор за духовым шкафом, фасад ПММ на двери машины.

Допущения и предложения на листе

Основа листа: взаимное расположение помещений, контур дома 9600 × 8000 и раскладка этажей подобраны проектировщиком под габариты помещений брифа; обмер и проект АР — задание (К-1); высота потолка 2900 мм — по брифу, не замерена; перекрытие 330 мм и отметка 2-го этажа +3,230 приняты; проект КР — задание (К-2); наружные стены 400 мм, перегородки 120 мм приняты (в брифе толщин нет) (К-1); разрешённая мощность 15 кВт принята по типовым ТУ для частного дома (К-4).
См. лист открытых вопросов (лист 6, записи К-1, К-2, К-4).

1000 мм · печать 1:1

						ГД-2026-012-АИ	
						Дом 120 м²	
						Общая площадь 147,36* м² · * размеры приняты, не замерены (реестр — л. 6, К-1)	
Изм.	Кол.уч	Лист	№ док.	Подп.	Дата	Дизайн-проект интерьера	Стадия: РП; Лист: 85; Листов: 130
Разраб.		Кырлан А.С.			19.10.26		
Пров.							
ГИП							
Н. контр.						**Кухня (пом. 1). Развёртка гарнитура**	**Кырлан Александр Сергеевич**
Утв.						М 1:25	

выпуск 19.10.2026 № 53e4f7ddae · стр. 90 из 160

Кухня (пом. 1). Монтажная схема

Гостиная-кухня (пом. 1) · стена А · размеры в мм от чистых поверхностей, высоты — от чистого пола

ПРЕДВАРИТЕЛЬНО · не для производства работ · открыто пунктов: 6 (реестр — л. 6)

Привязка выводов и крепление модулей

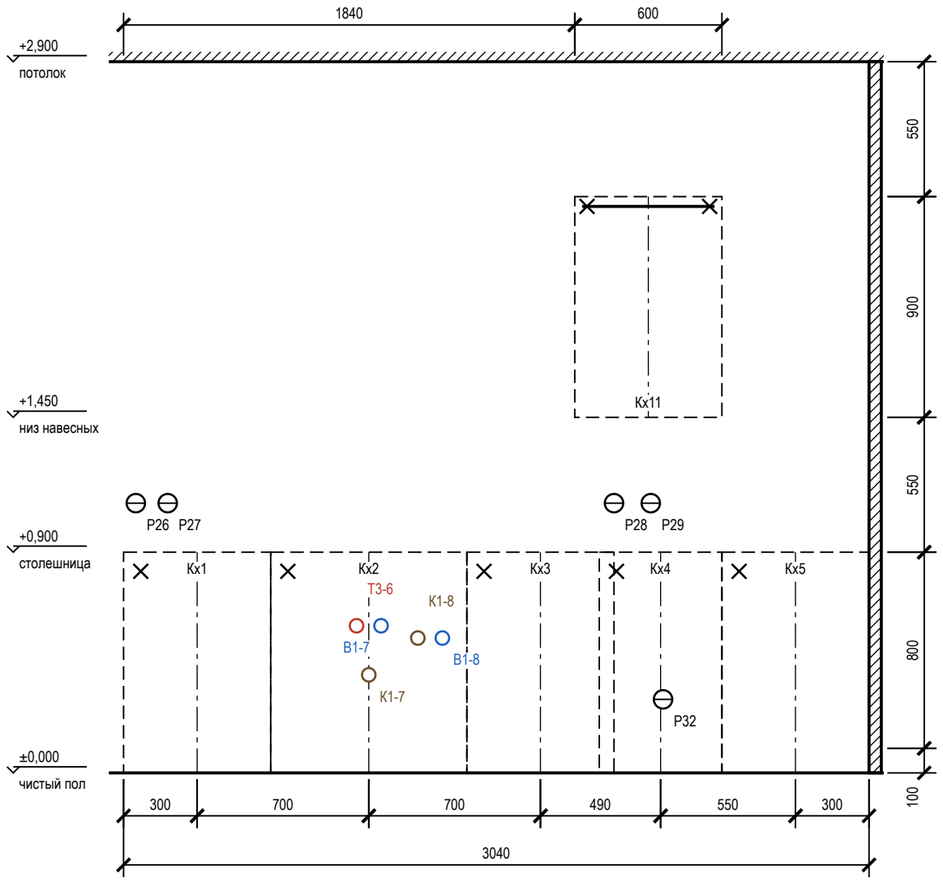

План столешницы

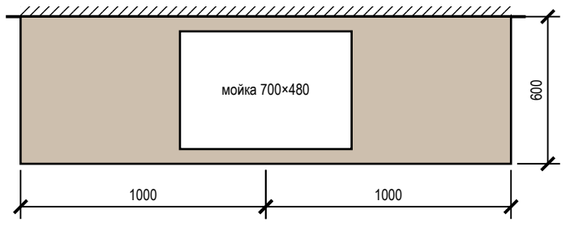

Привязка выводов к осям модулей

Код	Назначение	Модуль	От оси, мм	Н, мм	Размещение
Р26	розетка ×2 — фартук	Кх1	−250	1100	над столешницей (фартук)
Р27	розетка — фартук	Кх1	−120	1100	над столешницей (фартук)
Т3-6	Т3 — межос. 100	Кх2	−50	600	в модуле мойки
К1-7	К1 Ø50 — мойка	Кх2	0	400	в модуле мойки
В1-7	В1 — межос. 100	Кх2	+50	600	в модуле мойки
К1-8	К1 Ø40 — слив ПММ в шкафу мойки	Кх2	+200	550	в модуле мойки
В1-8	В1 — кран ПММ в шкафу мойки	Кх2	+300	550	в модуле мойки
Р28	розетка ×2 — фартук	Кх3	+300	1100	над столешницей (фартук)
Р29	розетка — фартук	Кх4	−40	1100	над столешницей (фартук)
Р32	розетка — посудомоечная машина	Кх4	+10	300	в соседнем модуле, за ящиком

Зазоры под отделку

Поверхность	Отделка	Зазор, мм	Учесть
фартук	керамогранит	10	от чернового основания до корпуса навесных и столешницы
стены	окраска	5	под штукатурку и шпаклёвку за пеналом
пол	инженерная доска		цоколь — после укладки пола, опоры ±20 мм

Условные обозначения

- навесной модуль (невидимый контур)
- ось модуля (от неё — привязка вывода)
- анкер / уголок крепления к стене
- розетка на стене
- вывод кабеля к технике
- В1 — вывод воды В1 / Т3, канализации К1

Примечания

1. Выводы — по проекту электрики и ВК; привязка по горизонтали — от оси модуля (плюс — вправо по виду), по высоте — от чистого пола до оси вывода.
2. Пенал — уголки к стене 2 шт. сверху; нижние модули — стяжками между собой и уголком к стене; ряд выставить по уровню опорами цоколя.
3. Розетки над столешницей — не ниже 150 мм над ней и не за корпусом техники; розетка за ПММ, духовым шкафом и холодильником — только в соседнем модуле или в зоне цоколя с доступом.
4. Столешница — вырезы по шаблонам выбранных моделей мойки и варочной панели; торцы у стены — герметик, пристеночный плинтус.

Допущения и предложения на листе

Основа листа: взаимное расположение помещений, контур дома 9600 × 8000 и раскладка этажей подобраны проектировщиком под габариты помещений брифа; обмер и проект АР — задание (К-1); высота потолка 2900 мм — по брифу, не замерена; перекрытие 330 мм и отметка 2-го этажа +3,230 приняты; проект КР — задание (К-2); наружные стены 400 мм, перегородки 120 мм приняты (в брифе толщин нет) (К-1); разрешённая мощность 15 кВт принята по типовым ТУ для частного дома (К-4).
См. лист открытых вопросов (лист 6, записи К-1, К-2, К-4).

1000 мм · печать 1:1

Изм.	Кол.уч	Лист	№ док.	Подп.	Дата
Разраб.		Кырлан А.С.			19.10.26
Пров.					
ГИП					
Н. контр.					
Утв.					

ГД-2026-012-АИ

Дом 120 м²

Общая площадь 147,36* м² · * размеры приняты, не замерены (реестр — л. 6, К-1)

Дизайн-проект интерьера	Стадия	Лист	Листов
	РП	86	130

Кухня (пом. 1). Монтажная схема

М 1:25

Кырлан Александр Сергеевич

выпуск 19.10.2026 № 53e4f7ddae · стр. 91 из 160

Кухня (пом. 1). Развёртка гарнитура

Гостиная-кухня (пом. 1) · стена Б · вид из помещения · размеры в мм, отметки в м

Вид с фасадами

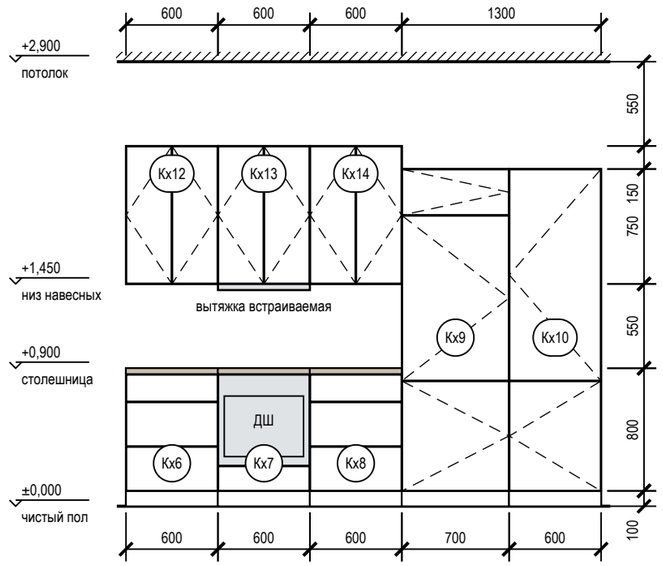

Вид без фасадов (наполнение, выводы)

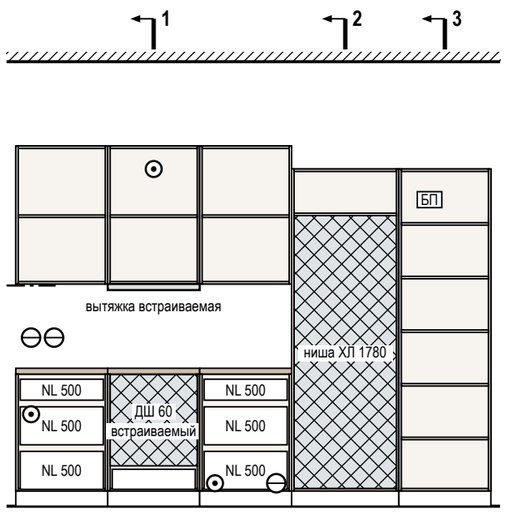

Разрез 1-1

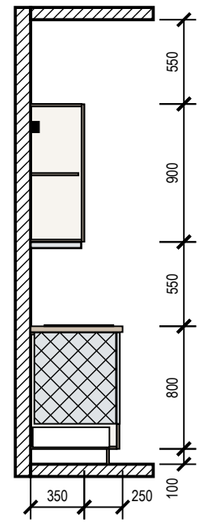

Разрез 2-2

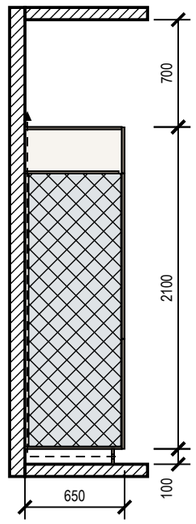

Разрез 3-3

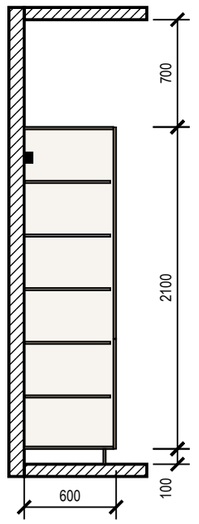

Условные обозначения

- фасад распашной: линии сходятся к стороне петель
- фасад ящика, карго
- встраиваемая техника
- столешница
- доборная планка
- деталь в разрезе
- К1 — марка модуля
- розетка на стене
- вывод кабеля к технике
- В1 — вывод воды В1 / Т3, канализации К1

Примечания

1. Размеры — в мм по чистовой отделке, вид из помещения; марки — как на плане расстановки. Перед раскроем — контрольный замер цеха после фартука и пола.
2. Корпуса — ЛДСП 16 мм, задняя стенка ХДФ 4 мм; фасады — МДФ, эмаль матовая 18 мм, цвет по колерной карте; столешница 38 мм, свес 20 мм; цоколь 100 мм.
3. Кромка: скрытые торцы 0,4 мм, видимые 2 мм. Номинальные зазоры: между фасадами 3 мм, фасад — столешница 3 мм, фасад — стена не менее 3 мм.
4. Ящики полного выдвижения и петли — с доводчиком; присадка по 32-й системе — выполняет цех.
5. Вытяжка встраивается в навесной модуль над варочной: её низ 510 мм над панелью — меньше 650 мм, модуль поднять или принять вытяжку с допуском по паспорту модели.
6. Ниши техники (холодильник — ориентир 1780 мм) — по монтажным схемам выбранных моделей: решётка в цоколе и канал за пеналом холодильника, зазор за духовым шкафом, фасад ПММ на двери машины.

Допущения и предложения на листе

Основа листа: взаимное расположение помещений, контур дома 9600 × 8000 и раскладка этажей подобраны проектировщиком под габариты помещений брифа; обмер и проект АР — задание (К-1); высота потолка 2900 мм — по брифу, не замерена; перекрытие 330 мм и отметка 2-го этажа +3,230 приняты; проект КР — задание (К-2); наружные стены 400 мм, перегородки 120 мм приняты (в брифе толщин нет) (К-1); разрешённая мощность 15 кВт принята по типовым ТУ для частного дома (К-4).

См. лист открытых вопросов (лист 6, записи К-1, К-2, К-4).

1000 мм · печать 1:1

Изм.	Кол.уч	Лист	№ док.	Подп.	Дата
Разраб.		Кырлан А.С.			19.10.26
Пров.					
ГИП					
Н. контр.					
Утв.					

ГД-2026-012-АИ

Дом 120 м²

Общая площадь 147,36* м² · * размеры приняты, не замерены (реестр — л. 6, К-1)

Дизайн-проект интерьера

Стадия	Лист	Листов
РП	87	130

Кухня (пом. 1). Развёртка гарнитура

М 1:40

Кырлан Александр Сергеевич

выпуск 19.10.2026 № 53e4f7ddae · стр. 92 из 160

Кухня (пом. 1). Монтажная схема

Гостиная-кухня (пом. 1) · стена Б · размеры в мм от чистых поверхностей, высоты — от чистого пола

ПРЕДВАРИТЕЛЬНО · не для производства работ · открыто пунктов: 6 (реестр — л. 6)

Привязка выводов и крепление модулей

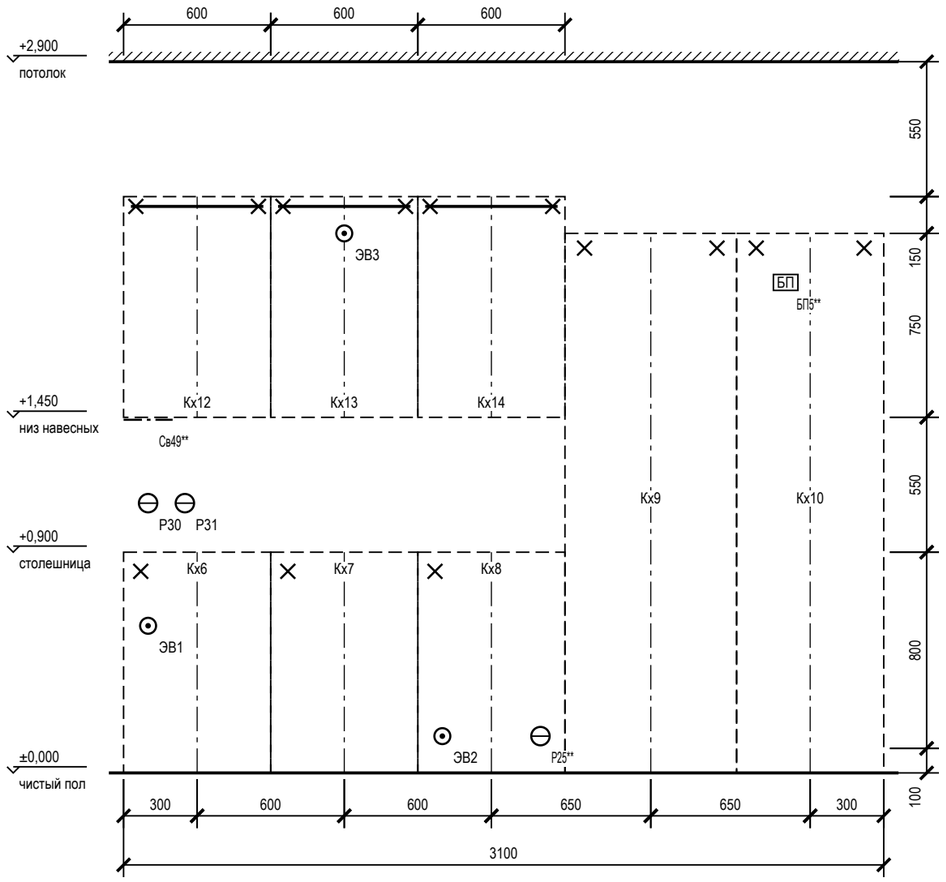

План столешницы

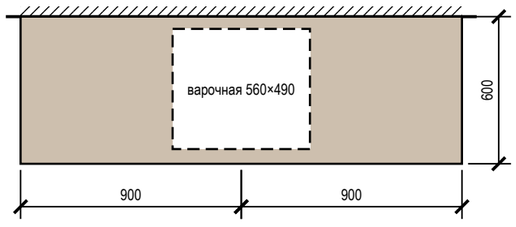

Привязка выводов к осям модулей

Код	Назначение	Модуль	От оси, мм	Н, мм	Размещение
Р30	розетка ×2 — фартук между мойкой и варочной	Кх6	−200	1100	над столешницей (фартук)
ЭВ1	вывод кабеля — варочная панель (в соседнем модуле М8.3, за ящиком)	Кх6	−200	600	в соседнем модуле, за ящиком
Св49**	светодиодная лента — подсветка столешницы	Кх6	−200	1440	в профиле по низу навесного модуля
Р31	розетка — фартук между мойкой и варочной	Кх6	−50	1100	над столешницей (фартук)
ЭВ3	вывод кабеля — вытяжка	Кх13	0	2200	в навесном модуле
ЭВ2	вывод кабеля — духовой шкаф	Кх8	−200	150	в соседнем модуле, за ящиком
Р25**	розетка — холодильник Кх9 (розетка в соседнем модуле Кх8, съёмная панель)	Кх8	+200	150	в соседнем модуле, за ящиком
БП5**	блок питания — в пенале М6, верх, съёмная панель	Кх10	−100	2000	за пеналом

Зазоры под отделку

Поверхность	Отделка	Зазор, мм	Учесть
фартук	керамогранит	10	от чернового основания до корпуса навесных и столешницы
стены	окраска	5	под штукатурку и шпаклёвку за пеналом
пол	инженерная доска		цоколь — после укладки пола, опоры ±20 мм

Условные обозначения

- навесной модуль (невидимый контур)
- ось модуля (от неё — привязка вывода)
- анкер / уголок крепления к стене
- розетка на стене
- вывод кабеля к технике
- B1 — вывод воды В1 / Т3, канализации К1

Примечания

1. Выводы — по проекту электрики и ВК; привязка по горизонтали — от оси модуля (плюс — вправо по виду), по высоте — от чистого пола до оси вывода.
2. Пенал — уголки к стене 2 шт. сверху; нижние модули — стяжками между собой и уголком к стене; ряд выставить по уровню опорами цоколя.
3. Розетки над столешницей — не ниже 150 мм над ней и не за корпусом техники; розетка за ПММ, духовым шкафом и холодильником — только в соседнем модуле или в зоне цоколя с доступом.
4. Столешница — вырезы по шаблонам выбранных моделей мойки и варочной панели; торцы у стены — герметик, пристеночный плинтус.

Допущения и предложения на листе

Основа листа: взаимное расположение помещений, контур дома 9600 × 8000 и раскладка этажей подобраны проектировщиком под габариты помещений брифа; обмер и проект АР — задание (К-1); высота потолка 2900 мм — по брифу, не замерена; перекрытие 330 мм и отметка 2-го этажа +3,230 приняты; проект КР — задание (К-2); наружные стены 400 мм, перегородки 120 мм приняты (в брифе толщин нет) (К-1); разрешённая мощность 15 кВт принята по типовым ТУ для частного дома (К-4).

Знак «**» — предложение проектировщика, заказчиком не утверждено (согласовать с заказчиком): записи в реестре нет: Р25 — высота 2000 мм выше нормы 1 м (ПУЭ 6.6.30) по назначению: питание встроенного холодильника М6, розетка над нишей за съёмной панелью; Св49, БП5 — диммируемость добавлена разработчиком проекта под светорегуляторы S11 и S12.

См. лист открытых вопросов (лист 6, записи К-1, К-2, К-4).

1000 мм · печать 1:1

Изм.	Кол.уч	Лист	№ док.	Подп.	Дата
Разраб.		Кырлан А.С.			19.10.26
Пров.					
ГИП					
Н. контр.					
Утв.					

ГД-2026-012-АИ

Дом 120 м²

Общая площадь 147,36* м² · * размеры приняты, не замерены (реестр — л. 6, К-1)

Дизайн-проект интерьера	Стадия	Лист	Листов
	РП	88	130

Кухня (пом. 1). Монтажная схема

М 1:25

Кырлан Александр Сергеевич

выпуск 19.10.2026 № 53e4f7ddae · стр. 93 из 160

Шкафы. Монтажная схема. Лист 1 из 2

крепление к стене, установочные размеры, зазоры под отделку · размеры в мм

ПРЕДВАРИТЕЛЬНО · не для производства работ · открыто пунктов: 6 (реестр — л. 6)

Шкаф-купе Пр1 (пом. 5)

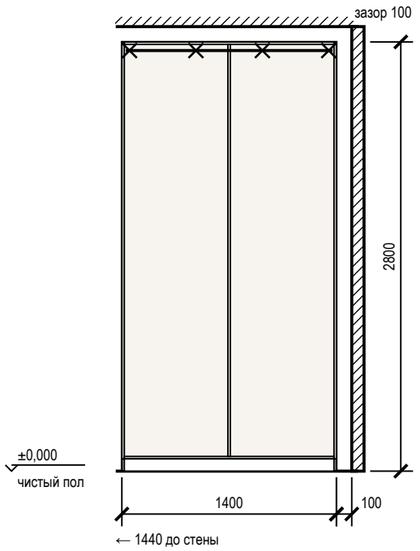

Шкаф распашной М4 (пом. 6)

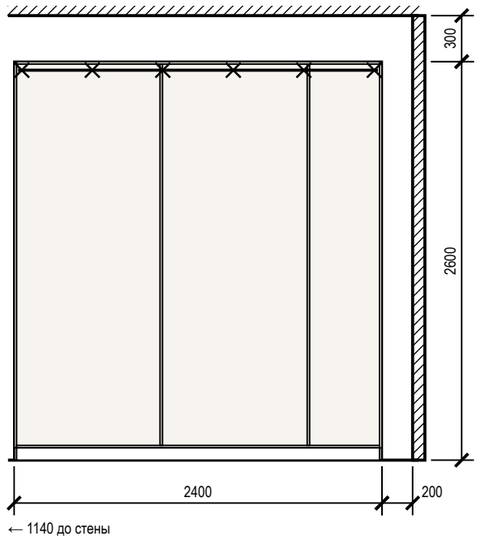

Шкаф распашной Д3 (пом. 7)

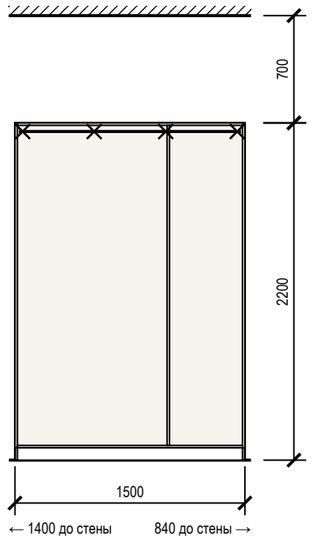

Система хранения Гд1 (пом. 8)

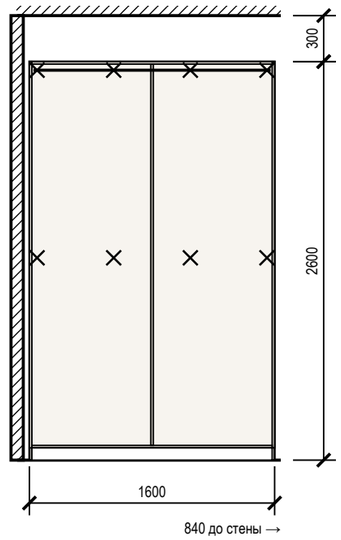

Система хранения Гд2 пом. 8

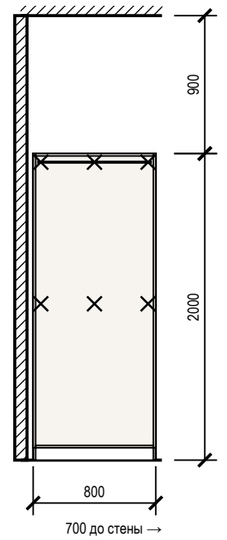

Крепление и зазоры под отделку (изделия листа 1)

Марка	Помещение, стена	Основание	Отделка стены	Зазор, мм	Крепёж по планке	От опрокидывания
Пр1	Прихожая (5), стена Б	по основанию — см. таблицу крепежа	окраска	5	анкер 4 шт., шаг 433	уголки 2 шт.
М4	Спальня родителей (6), стена В	по основанию — см. таблицу крепежа	окраска	5	анкер 6 шт., шаг 460	уголки 2 шт.
Д3	Детская (7), стена А	по основанию — см. таблицу крепежа	окраска	5	анкер 4 шт., шаг 467	уголки 2 шт.
Гд1	Гардеробная (8), стена А	по основанию — см. таблицу крепежа	окраска	5	анкер 8 шт. (2 ряда)	true
Гд2	Гардеробная (8), стена Г	по основанию — см. таблицу крепежа	окраска	5	анкер 6 шт. (2 ряда)	true

Крепёж по основанию стены

Основание стены	Крепёж
бетон, ж/б	анкер-шуруп 7,5×72 или дюбель 8×60 с шурупом 5×70
кирпич полнотелый	дюбель 8×80 с шурупом 5×90
газобетон, пазогребень	дюбель для газобетона 10×100 или химический анкер
гипсокартон	закладная до обшивки (брус 40×80 или фанера 18 мм), саморез в закладную

Условные обозначения

- анкер / уголок крепления к стене
- корпус и полки ЛДСП (вид на стену)
- компенсатор — короб до потолка

Примечания

1. Установочные размеры — от чистого пола и чистых стен; перед установкой контрольный замер после отделки.
2. Порядок: корпус выставить по уровню опорами цоколя → закрепить к стене по задней планке → навесить двери и фасады, отрегулировать зазоры → подогнать и закрепить компенсатор.
3. Анкеры — с шагом не более 500 мм, не ближе 50 мм от края планки; на ГКЛ только в закладную, установленную до обшивки.
4. Скрытые коммуникации под анкеры проверить детектором; трассы электрики по плану розеток.
5. Монтажная схема на 2 листах, лист 1 из 2; продолжение — на следующем листе схемы. Условные обозначения, таблица крепежа по основанию и примечания повторены на каждом листе.

Допущения и предложения на листе

Основа листа: взаимное расположение помещений, контур дома 9600 × 8000 и раскладка этажей подобраны проектировщиком под габариты помещений брифа; обмер и проект АР — задание (К-1); высота потолка 2900 мм — по брифу, не замерена; перекрытие 330 мм и отметка 2-го этажа +3,230 приняты; проект КР — задание (К-2); наружные стены 400 мм, перегородки 120 мм приняты (в брифе толщин нет) (К-1); разрешённая мощность 15 кВт принята по типовым ТУ для частного дома (К-4).
См. лист открытых вопросов (лист 6, записи К-1, К-2, К-4).

1000 мм · печать 1:1

Изм.	Кол.уч	Лист	№ док.	Подп.	Дата
Разраб.		Кырлан А.С.			19.10.26
Пров.					
ГИП					
Н. контр.					
Утв.					

ГД-2026-012-АИ

Дом 120 м²

Общая площадь 147,36* м² · * размеры приняты, не замерены (реестр — л. 6, К-1)

Дизайн-проект интерьера

Стадия	Лист	Листов
РП	89	130

Шкафы. Монтажная схема. Лист 1 из 2

М 1:40

Кырлан Александр Сергеевич

выпуск 19.10.2026 № 53e4f7ddae · стр. 94 из 160

Шкафы. Монтажная схема. Лист 2 из 2

крепление к стене, установочные размеры, зазоры под отделку · размеры в мм

ПРЕДВАРИТЕЛЬНО · не для производства работ · открыто пунктов: 6 (реестр — л. 6)

Система хранения Кл1 (пом. 9)

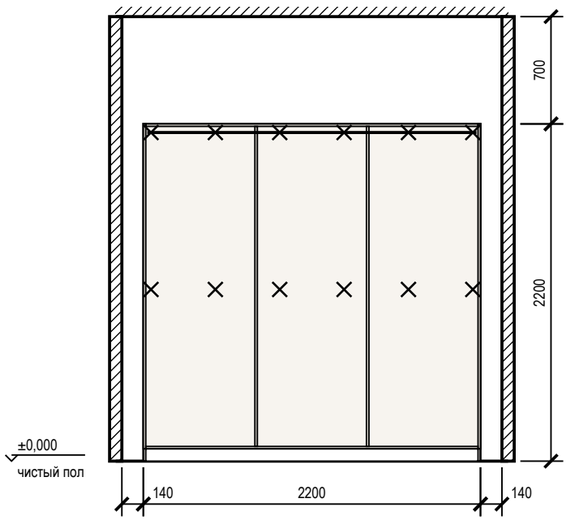

Система хранения Кл2 пом. 9

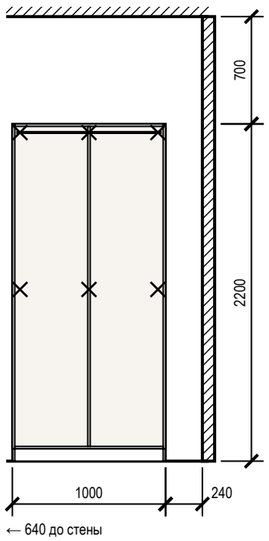

Шкаф распашной Д8 (пом. 12)

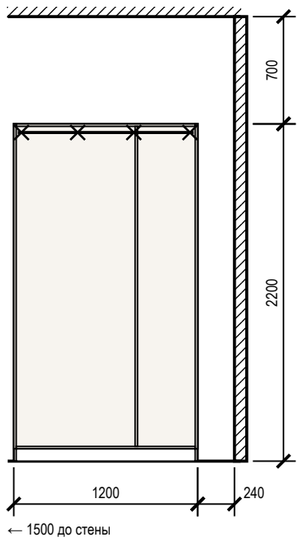

Система хранения Д10 пом. 12

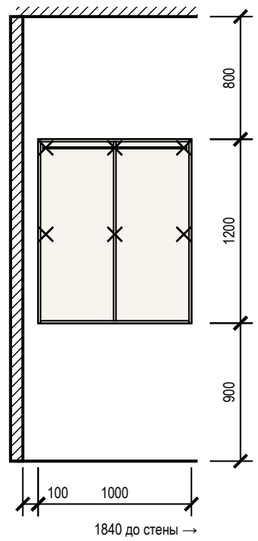

Крепление и зазоры под отделку (изделия листа 2)

Марка	Помещение, стена	Основание	Отделка стены	Зазор, мм	Крепёж по планке	От опрокидывания
Кл1	Кладовая (9), стена В	по основанию — см. таблицу крепежа	окраска	5	анкер 12 шт. (2 ряда)	true
Кл2	Кладовая (9), стена Г	по основанию — см. таблицу крепежа	окраска	5	анкер 6 шт. (2 ряда)	true
Д8	Детская вторая (12), стена Г	по основанию — см. таблицу крепежа	окраска	5	анкер 4 шт., шаг 367	уголки 2 шт.
Д10	Детская вторая (12), стена Г	по основанию — см. таблицу крепежа	окраска	5	анкер 6 шт. (2 ряда)	true

Крепёж по основанию стены

Основание стены	Крепёж
бетон, ж/б	анкер-шуруп 7,5×72 или дюбель 8×60 с шурупом 5×70
кирпич полнотелый	дюбель 8×80 с шурупом 5×90
газобетон, пазогребень	дюбель для газобетона 10×100 или химический анкер
гипсокартон	закладная до обшивки (брус 40×80 или фанера 18 мм), саморез в закладную

Условные обозначения

- анкер / уголок крепления к стене
- корпус и полки ЛДСП (вид на стену)
- компенсатор — короб до потолка

Примечания

1. Установочные размеры — от чистого пола и чистых стен; перед установкой контрольный замер после отделки.
2. Порядок: корпус выставить по уровню опорами цоколя → закрепить к стене по задней планке → навесить двери и фасады, отрегулировать зазоры → подогнать и закрепить компенсатор.
3. Анкеры — с шагом не более 500 мм, не ближе 50 мм от края планки; на ГКЛ только в закладную, установленную до обшивки.
4. Скрытые коммуникации под анкеры проверить детектором; трассы электрики по плану розеток.
5. Монтажная схема на 2 листах, лист 2 из 2. Условные обозначения, таблица крепежа по основанию и примечания повторены на каждом листе.

Допущения и предложения на листе

Основа листа: взаимное расположение помещений, контур дома 9600 × 8000 и раскладка этажей подобраны проектировщиком под габариты помещений брифа; обмер и проект АР — задание (К-1); высота потолка 2900 мм — по брифу, не замерена; перекрытие 330 мм и отметка 2-го этажа +3,230 приняты; проект КР — задание (К-2); наружные стены 400 мм, перегородки 120 мм приняты (в брифе толщин нет) (К-1); разрешённая мощность 15 кВт принята по типовым ТУ для частного дома (К-4).
См. лист открытых вопросов (лист 6, записи К-1, К-2, К-4).

1000 мм · печать 1:1

Изм.	Кол.уч	Лист	№ док.	Подп.	Дата
Разраб.		Кырлан А.С.			19.10.26
Пров.					
ГИП					
Н. контр.					
Утв.					

ГД-2026-012-АИ

Дом 120 м²

Общая площадь 147,36* м² · * размеры приняты, не замерены (реестр — л. 6, К-1)

Дизайн-проект интерьера

Стадия	Лист	Листов
РП	90	130

Шкафы. Монтажная схема. Лист 2 из 2

М 1:40

Кырлан Александр Сергеевич

выпуск 19.10.2026 № 53e4f7ddae · стр. 95 из 160

Ведомости изделий, техники и фурнитуры

встроенная мебель и кухонный гарнитур · размеры в мм

Ведомость изделий

Марка	Наименование	Пом.	Ш×Г×В, мм	Корпус	Фасад	Кромка, мм скр./вид.	Кол.
Пр1	Шкаф-купе	5	1400×600×2800	ЛДСП 16	рифлёные панели МДФ в алюминиевом профиле	0,4 / 2	1
М4	Шкаф распашной	6	2400×600×2600	ЛДСП 16	МДФ 18, эмаль матовая	0,4 / 2	1
Д3	Шкаф распашной	7	1500×600×2200	ЛДСП 16	МДФ 18, эмаль матовая	0,4 / 2	1
Гд1	Система хранения	8	1600×600×2600	ЛДСП 16	без фасадов; ящики — МДФ 18, эмаль матовая	0,4 / 2	1
Гд2	Система хранения	8	800×400×2000	ЛДСП 16	без фасадов; ящики — МДФ 18, эмаль матовая	0,4 / 2	1
Кл1	Система хранения	9	2200×400×2200	ЛДСП 16	без фасадов; ящики — МДФ 18, эмаль матовая	0,4 / 2	1
Кл2	Система хранения	9	1000×400×2200	ЛДСП 16	без фасадов; ящики — МДФ 18, эмаль матовая	0,4 / 2	1
Д8	Шкаф распашной	12	1200×600×2200	ЛДСП 16	МДФ 18, эмаль матовая	0,4 / 2	1
Д10	Система хранения	12	1000×300×1200	ЛДСП 16	без фасадов; ящики — МДФ 18, эмаль матовая	0,4 / 2	1
Кх1	Модуль нижний: ящики	1	600×600×900	ЛДСП 16	МДФ 18, эмаль матовая	0,4 / 2	1
Кх2	Модуль нижний: мойка	1	800×600×900	ЛДСП 16	МДФ 18, эмаль матовая	0,4 / 2	1
Кх3	Модуль нижний: ПММ	1	600×600×900	ЛДСП 16	МДФ 18, эмаль матовая	0,4 / 2	1
Кх11	Модуль навесной: полки	1	600×350×900	ЛДСП 16	МДФ 18, эмаль матовая	0,4 / 2	1
Кх4	Модуль нижний: ящики	1	500×600×900	ЛДСП 16	МДФ 18, эмаль матовая	0,4 / 2	1
Кх5	Модуль нижний: ящики	1	600×600×900	ЛДСП 16	МДФ 18, эмаль матовая	0,4 / 2	1
Кх6	Модуль нижний: ящики	1	600×600×900	ЛДСП 16	МДФ 18, эмаль матовая	0,4 / 2	1
Кх12	Модуль навесной: полки	1	600×350×900	ЛДСП 16	МДФ 18, эмаль матовая	0,4 / 2	1
Кх7	Модуль нижний: духовой шкаф, варочная	1	600×600×900	ЛДСП 16	МДФ 18, эмаль матовая	0,4 / 2	1
Кх13	Модуль навесной: полки	1	600×350×900	ЛДСП 16	МДФ 18, эмаль матовая	0,4 / 2	1
Кх8	Модуль нижний: ящики	1	600×600×900	ЛДСП 16	МДФ 18, эмаль матовая	0,4 / 2	1
Кх14	Модуль навесной: полки	1	600×350×900	ЛДСП 16	МДФ 18, эмаль матовая	0,4 / 2	1
Кх9	Пенал: холодильник встр.	1	700×650×2200	ЛДСП 16	МДФ 18, эмаль матовая	0,4 / 2	1
Кх10	Пенал: полки	1	600×600×2200	ЛДСП 16	МДФ 18, эмаль матовая	0,4 / 2	1

Ведомость встраиваемой техники

Поз.	Прибор	Ниша, вырез, мм	Вентиляция	Питание	Схема
Кх2	Мойка врезная / подстольная с сифоном	вырез по шаблону, ориентир 700 × 480		смеситель — выводы ВК	по модели
Кх3	Посудомоечная машина встраиваемая, 60 см	ниша 600 × 862 (от пола до низа столешницы)	зазор в цоколе, по схеме	розетка в соседнем модуле	по модели
Кх7	Духовой шкаф встраиваемый, 60 см	ниша 560 × 595, глубина ≥ 550	зазор за шкафом, вырез в задней стенке	вывод кабеля под шкафом	по модели
Кх7	Варочная панель индукционная, 60 см	вырез в столешнице 560 × 490		вывод кабеля под модулем	по модели
Кх9	Холодильник встраиваемый, ниша 1780	ниша 1780 × 560 × 550	решётка в цоколе, канал за корпусом, выход сверху	розетка над нишей или в соседнем модуле	по модели
Кх7	Вытяжка настенная, 60 см	низ ≥ 650 над панелью	воздуховод к вентканалу, короб до потолка	вывод кабеля в коробе	по модели

Примечания

1. Модели техники выбирает заказчик до изготовления мебели; ниши, вырезы и вентиляция — по монтажной схеме выбранной модели (условие гарантии), её номер вносится в ведомость.
2. Количество фурнитуры — по чертежам изделий; запас крепежа 5 %. Аналоги — по характеристикам (доводчик, нагрузка, ход).
3. Цвет корпусов, фасадов и профилей — по колерной карте проекта.

Ведомость фурнитуры

№	Фурнитура	Тип, размер	Изделия	Кол.
1	Система дверей купе: профиль, направляющие, ролики	на 2 двери	Пр1	1
2	Ручка-профиль вертикальная	в цвет профиля	Пр1	2
3	Полкодержатель с фиксацией	ø5 мм	Пр1, М4, Д3, Гд1, Кл1, Кл2, Д8, Д10, Кх11, Кх12, Кх13, Кх14, Кх9, Кх10	256
4	Штанга овальная 30×15, L = 676	+ 2 держателя	Пр1	1
5	Полка для обуви выдвижная наклонная	ширина 676	Пр1	3
6	Опора регулируемая с цоколем на клипсах	ход 20 мм	Пр1, М4, Д3, Гд1, Гд2, Кл1, Кл2, Д8	50
7	Анкер по основанию стены	по таблице крепежа	Пр1, М4, Д3, Гд1, Гд2, Кл1, Кл2, Д8, Д10, Кх11, Кх12, Кх13, Кх14	64
8	Уголок крепления к стене от опрокидывания	стальной	Пр1, М4, Д3, Гд1, Гд2, Кл1, Кл2, Д8, Д10, Кх9, Кх10	22
9	Петля накладная 110° с доводчиком	чашка 35 мм	М4, Д3, Д8, Кх2, Кх11, Кх12, Кх13, Кх14, Кх9, Кх10	98
10	Штанга овальная 30×15, L = 936	+ 2 держателя	М4	2
11	Штанга овальная 30×15, L = 456	+ 2 держателя	М4	1
12	Штанга овальная 30×15, L = 976	+ 2 держателя	Д3	1
13	Штанга овальная 30×15, L = 776	+ 2 держателя	Гд1, Д8	2
14	Штанга выдвижная торцевая	L по глубине	Гд2, Кл1, Кл2	5
15	Направляющие полного выдвижения с доводчиком NL 500	пара	Кх1, Кх4, Кх5, Кх6, Кх7, Кх8	16
16	Ручка-профиль	латунь матовая	Кх1, Кх2, Кх3, Кх11, Кх4, Кх5, Кх6, Кх12, Кх7, Кх13, Кх8, Кх14, Кх9, Кх10	32
17	Опора кухонная регулируемая 100–120 мм	+ клипса цоколя	Кх1, Кх2, Кх3, Кх4, Кх5, Кх6, Кх7, Кх8, Кх9, Кх10	44
18	Комплект навески фасада ПММ	из поставки машины	Кх3	1
19	Навес регулируемый для навесного шкафа	пара на секцию	Кх11, Кх12, Кх13, Кх14	4
20	Шина монтажная	L = 540	Кх11, Кх12, Кх13, Кх14	4

Допущения и предложения на листе

Основа листа: взаимное расположение помещений, контур дома 9600 × 8000 и раскладка этажей подобраны проектировщиком под габариты помещений брифа; обмер и проект АР — задание (К-1); высота потолка 2900 мм — по брифу, не замерена; перекрытие 330 мм и отметка 2-го этажа +3,230 приняты; проект КР — задание (К-2); наружные стены 400 мм, перегородки 120 мм приняты (в брифе толщин нет) (К-1); разрешённая мощность 15 кВт принята по типовым ТУ для частного дома (К-4).
См. лист открытых вопросов (лист 6, записи К-1, К-2, К-4).

Изм.	Кол.уч	Лист	№ док.	Подп.	Дата
Разраб.		Кырлан А.С.			19.10.26
Пров.					
ГИП					
Н. контр.					
Утв.					

ГД-2026-012-АИ

Дом 120 м²

Общая площадь 147,36* м² · * размеры приняты, не замерены (реестр — л. 6, К-1)

Дизайн-проект интерьера	Стадия	Лист	Листов
	РП	91	130

Ведомости изделий, техники и фурнитуры

М б/м

Кырлан Александр Сергеевич

04

Развёртки и узлы

Кырлан Александр Сергеевич

выпуск 19.10.2026 · 53e4f7ddae · стр. 97 из 160

Реестр марок отделки и позиций альбома

Реестр марок отделки (О ↔ позиции колерной карты) и марки позиций по видам

Реестр марок отделки альбома

Марка	Поверхность	Материал, изделие	Цвет, код	Помещения	Колер. карта
О1	стены	окраска, Farrow & Ball Modern Emulsion, матовая, подготовка Q3	Tikkurila G503 «Calla»	1, 2, 3, 5, 6, 7, 10, 11, 12	К1
О2	фартук	керамогранит, 1200×600×9 мм, аналог: керамогранит под травертин, матовый, затирка CG2WA		1	КМ2
О3	акцентная стена	окраска, Farrow & Ball Modern Emulsion, матовая, подготовка Q3	NCS S 3050-R80B «Эгейский синий»	1	К2
О4	плинтус	плинтус МДФ, h 80 мм, аналог: плинтус МДФ под покраску 80×16	Tikkurila G503 «Calla»	1, 2, 3, 5, 6, 10, 11	К4
О5	потолок	окраска, Tikkurila Anti-Reflex 2, глубокоматовая, подготовка Q3	Little Greene No. 222 «Loft White»	1, 2, 3, 5, 6, 7, 8, 10, 11, 12	К3
О6	пол	инженерная доска, Coswick Вековые традиции, 2100×127 мм, 1167-4250		1, 2, 3, 6, 7, 8, 9, 10, 11, 12	КМ1
О7	акцентная стена	окраска, Farrow & Ball Modern Emulsion, матовая, подготовка Q3	NCS S 5020-G90Y «Олива»	3	К5
О8	стены	облицовка плиткой, Atlas Concorde Marvel Travertine, 600×1200×9 мм, A8UZ, затирка CG2WA	Atlas Concorde A8UZ «Marvel Travertine»	4, 13	К6
О9	потолок	окраска, Tikkurila Luja 7, матовая, подготовка Q3	Little Greene No. 222 «Loft White»	4, 13	К7
О10	пол	керамогранит, Atlas Concorde Marvel Travertine, 600×1200×9 мм, A8UZ, затирка CG2WA	Atlas Concorde A8UZ «Marvel Travertine»	4, 5, 13	К6
О11	акцентная стена	окраска, Farrow & Ball Modern Emulsion, матовая, подготовка Q3	Farrow & Ball No. 89 «Lulworth Blue светлая морская лазурь»	6	К8
О12	акцентная стена	окраска, Farrow & Ball Modern Emulsion, матовая, подготовка Q3	Farrow & Ball No. 66 «India Yellow — охра / горчица итальянских фасадов»	7	К9
О13	плинтус	плинтус МДФ, Orac Decor Contour (Luxxus), h 69 мм, SX165	Tikkurila G503 «Calla»	7, 12	К10
О14	стены	окраска, Tikkurila Harmony, матовая, подготовка Q3	Little Greene No. 222 «Loft White»	8	К11
О15	плинтус	плинтус МДФ, h 80 мм, аналог: плинтус МДФ под покраску 80×16	Little Greene No. 222 «Loft White»	8	К12
О16	стены	окраска, Tikkurila, матовая, подготовка Q3	NCS S 0502-Y	9	К13
О17	плинтус	плинтус МДФ, Orac Decor Contour (Luxxus), h 69 мм, SX165, шелковисто-матовая	NCS S 0300-N	9	К15
О18	потолок	окраска, Tikkurila, глубокоматовая	NCS S 0300-N	9	К14
О19	акцентная стена	окраска, Farrow & Ball Modern Emulsion, матовая, подготовка Q3	Tikkurila H440 «H440 Wave — бирюзово-голубая вода»	12	К16

Марки позиций альбома по видам

Префикс	Что обозначает, позиции	Листы
Д, Д-вх	двери: Д-1–Д-10, Д-вх	13–19
Пр	проёмы без полотна (порталы): Пр-1	13–19
ОК	окна: ОК-1–ОК-6	13–19
Гд, Гс, Д, Кб, Кл, Кх, М, Пр, Хл	мебель и оборудование: Гд1, Гд2, Гс1–Гс5, Д1–Д10, Кб1–Кб4, Кл1, Кл2, Кх1–Кх15, М1–М6, Пр1, Пр2, Хл1, Хл2	20–27
Сг, См	сантехнические приборы: Сг1, Сг2, См1–См5	46–50
ДК	декор (картины, зеркала, растения): ДК1–ДК12, ДК40, ДК41, ДК43–ДК46	1, 67–73
Т	текстиль (шторы, ковры): Т1–Т31	1, 67–73
S	выключатели: S1–S5, S7–S10, S11**, S12**, S14–S16, S81, S84	28–41
Р	розетки: Р1–Р6, Р7**, Р8**, Р9–Р11, Р13–Р16, Р17**, Р18**, Р19**, Р20–Р24, Р25**, Р26–Р32, Р33**, Р34, Р40	28–41
ТВ	розетки ТВ: ТВ1	28–41
LAN	розетки компьютерные: LAN2, LAN3	28–41
ЭВ	выводы кабеля: ЭВ1–ЭВ3, ЭВ4**, ЭВ5**, ЭВ6**	28–41
АР	точки доступа Wi-Fi: АР1**, АР2**	28–41
Св	светильники: Св1–Св24, Св26–Св41, Св42**, Св43**, Св44**, Св45–Св48, Св49**, Св50–Св54, Св80, Св82–Св85	28–41
БП	блоки питания LED: БП1–БП4, БП5**	28–41
ИП	извещатели: ИП1–ИП7	28–41
КУП	электроустановочные изделия: КУП1**, КУП2**	28–41
ЩК, ЩС**	щиты: ЩК, ЩС**	28–41
ДФ	домофон: ДФ1	28–41
Ст В1, Ст К1, Ст К1-2 (кухня), Ст Т3	стояки (системы В1, Т3, К1): Ст В1-1, Ст В1-2, Ст К1-1, Ст К1-2 (кухня), Ст Т3-1, Ст Т3-2	46–50
О	марки отделки (реестр альбома): О1–О19	2–5, 92–123
К, КМ	позиции колерной карты: К1–К16, КМ1, КМ2	62–66
Рд	радиаторы отопления: Рд1, Рд3–Рд8	42–45

Допущения и предложения на листе. Основа листа: взаимное расположение помещений, контур дома 9600 × 8000 и раскладка этажей подобраны проектировщиком под габариты помещений брифа; обмер и проект АР — задание (К-1); высота потолка 2900 мм — по брифу, не замерена; перекрытие 330 мм и отметка 2-го этажа +3,230 приняты; проект КР — задание (К-2); наружные стены 400 мм, перегородки 120 мм приняты (в брифе толщин нет) (К-1); разрешённая мощность 15 кВт принята по типовым ТУ для частного дома (К-4). Знак «**» — предложено, не утверждено (согласовать): записи в реестре нет: плинтус пом. 1–3, 5, 6, 8, 10, 11, фартук пом. 1, S11, S12, Р18, Р19, Р25, Св42, Св43, Св44, Св49, БП5, Р33, ЭВ5, КУП2, Р17, Р7, Р8, ЭВ4, КУП1, ЭВ6, АР2, ЩС, АР1. См. лист открытых вопросов (лист 6, записи К-1, К-2, К-4).

Изм.	Кол.уч	Лист	№ док.	Подп.	Дата
Разраб.		Кырлан А.С.			19.10.26
Пров.					
ГИП					
Н. контр.					
Утв.					

ГД-2026-012-АИ

Дом 120 м²

Общая площадь 147,36* м² · * размеры приняты, не замерены (реестр — л. 6, К-1)

Дизайн-проект интерьера

Стадия	Лист	Листов
РП	92	130

Реестр марок отделки и позиций альбома

М б/м

Кырлан Александр Сергеевич

выпуск 19.10.2026 № 53e4f7ddae · стр. 98 из 160

Реестр марок отделки и позиций альбома (продолжение)

Реестр марок отделки (О ↔ позиции колерной карты) и марки позиций по видам

Примечания

1. Марка отделки О — одна на весь альбом: одна и та же отделка (материал, изделие, цвет, формат) на всех листах имеет одну марку; на развёртках и планах стоят марки этого реестра.
2. Столбец «Колер. карта» — позиции колерной карты (лист 62): К — окраска по коду цвета, КМ — материал без кода цвета; «Помещения» — номера по экспликации; количества — по ведомости отделки помещений (лист 60).
3. Марки позиций: один префикс — один вид позиций на весь альбом (двери Д, окна ОК, мебель М, сантехприборы П, декор ДК, текстиль Т, колерная карта К и КМ, радиаторы РО, розетки Р, выключатели S, светильники Св; стояки — «Ст» и система, например «Ст К1-1»). Совпадение префиксов у разных видов — замечание к исходным данным, при выпуске исправляется в модели.

Допущения и предложения на листе

Основа листа: взаимное расположение помещений, контур дома 9600 × 8000 и раскладка этажей подобраны проектировщиком под габариты помещений брифа; обмер и проект АР — задание (К-1); высота потолка 2900 мм — по брифу, не замерена; перекрытие 330 мм и отметка 2-го этажа +3,230 приняты; проект КР — задание (К-2); наружные стены 400 мм, перегородки 120 мм приняты (в брифе толщин нет) (К-1); разрешённая мощность 15 кВт принята по типовым ТУ для частного дома (К-4).
Знак «**» — предложение проектировщика, заказчиком не утверждено (согласовать с заказчиком): записи в реестре нет: плинтус пом. 1–3, 5, 6, 8, 10, 11, фартук пом. 1 — артикул изделия не выбран: позиция описана характеристиками («аналог по характеристикам»), артикул выбирается при закупке.
См. лист открытых вопросов (лист 6, записи К-1, К-2, К-4).

Изм.	Кол.уч	Лист	№ док.	Подп.	Дата
Разраб.		Кырлан А.С.			19.10.26
Пров.					
ГИП					
Н. контр.					
Утв.					

ГД-2026-012-АИ

Дом 120 м²

Общая площадь 147,36* м² · * размеры приняты, не замерены (реестр — л. 6, К-1)

Дизайн-проект интерьера	Стадия	Лист	Листов
	РП	93	130
Реестр марок отделки и позиций альбома (продолжение) М б/м	**Кырлан Александр Сергеевич**		

выпуск 19.10.2026 № 53e4f7ddae · стр. 99 из 160

Схема расположения развёрток и узлов

План квартиры: марки развёрток по помещениям, выноски узлов, ведомость «марка → лист»

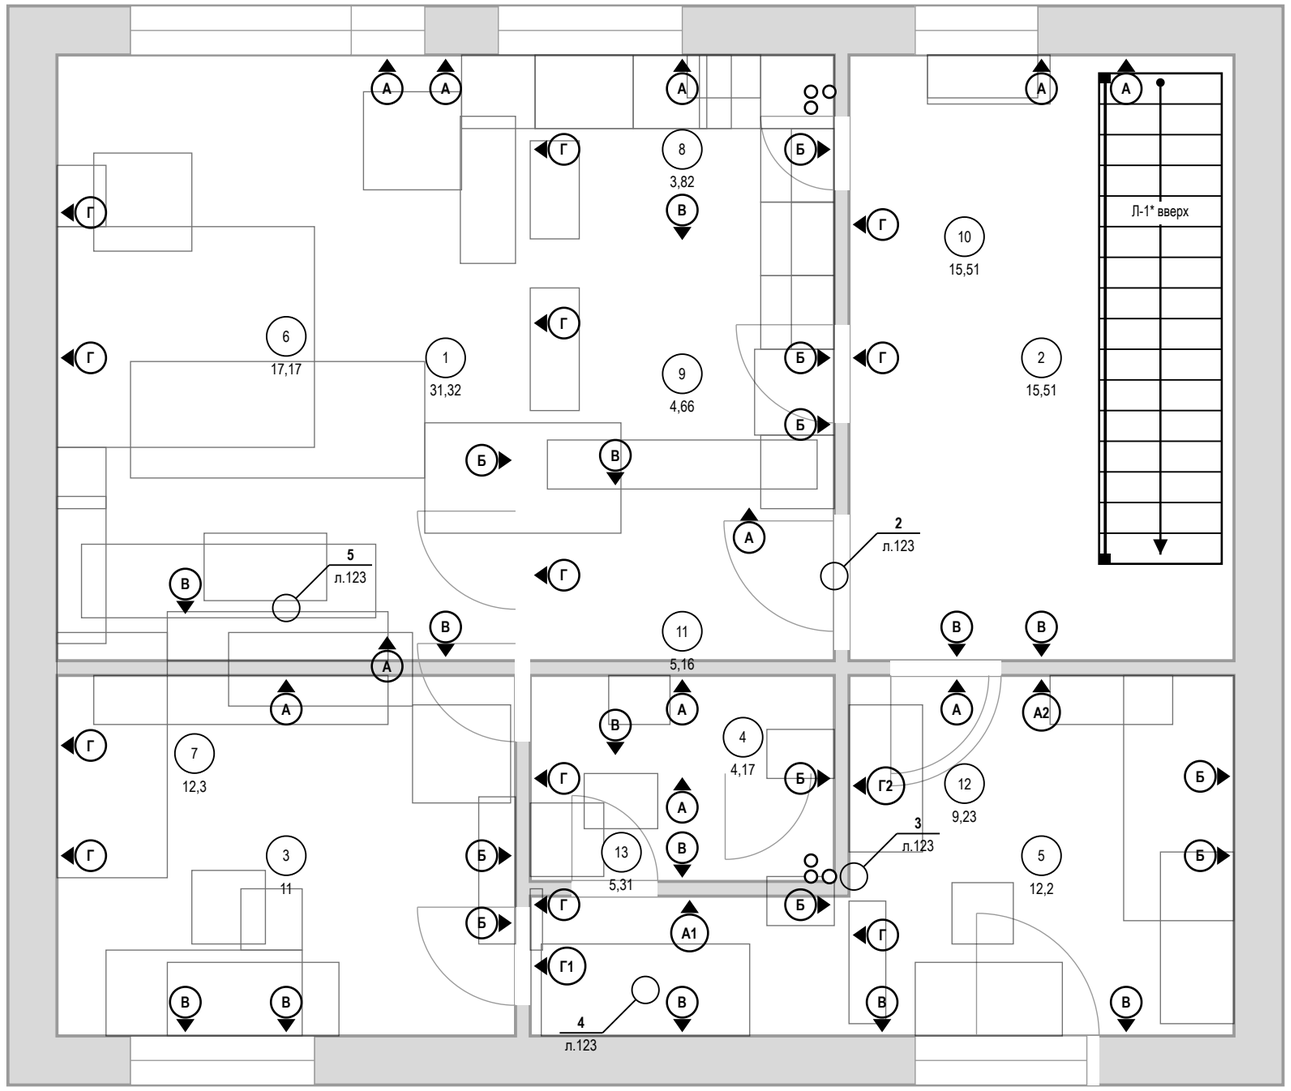

Допущения и предложения на листе. Основа листа: взаимное расположение помещений, контур дома 9600 × 8000 и раскладка этажей подобраны проектировщиком под габариты помещений брифа; обмер и проект АР — задание (К-1); высота потолка 2900 мм — по брифу, не замерена; перекрытие 330 мм и отметка 2-го этажа +3,230 приняты; проект КР — задание (К-2); наружные стены 400 мм, перегородки 120 мм приняты (в брифе толщин нет) (К-1); разрешённая мощность 15 кВт принята по типовым ТУ для частного дома (К-4). Знак «*» — принято, не замерено и не подтверждено (замерить на объекте): К-3: Л-1 — место, тип и размеры лестницы брифом не заданы (только «лестница из холла 1-го этажа»): одномаршевая 17 × 190 × 250 вдоль стены Б холла — предложение проектировщика; конструкция и расчёт — проект КР. См. лист открытых вопросов (лист 6, записи К-1–К-4).

Условные обозначения

- А — марка развёртки: буква стены, стрелка — взгляд
- выноска узла: над полкой — узел, под полкой — лист
- 1 — номер помещения, площадь м²

1000 мм · печать 1:1

Примечания

1. Развёртки — вид на стену изнутри помещения; буквы стен — одна система на весь альбом (как на листах выводов, плитки и отделки).
2. Стены без электроточек, мебели, декора и акцентной отделки развёрток не имеют: их отделка — по ведомости отделки помещений.
3. Узлы — на листе узлов; места применения — по выноскам этого листа и ведомости «марка → лист».

ПРЕДВАРИТЕЛЬНО · не для производства работ · открыто пунктов: 6 (реестр — л. 6)

Развёртки и узлы: марка → лист

Марка	Помещение / узел	Лист
А	Гостиная-кухня (пом. 1)	95
Б	Гостиная-кухня (пом. 1)	96
В	Гостиная-кухня (пом. 1)	97
Г	Гостиная-кухня (пом. 1)	98
А, В	Холл с лестницей (пом. 2)	99
Г	Холл с лестницей (пом. 2)	100
А, Б	Кабинет (пом. 3)	101
В, Г	Кабинет (пом. 3)	102
А, Б	Санузел гостевой (пом. 4)	103
В, Г	Санузел гостевой (пом. 4)	104
А1, А2, Б	Прихожая (пом. 5)	105
В, Г1, Г2	Прихожая (пом. 5)	106
А, Б	Спальня родителей (пом. 6)	107
В, Г	Спальня родителей (пом. 6)	108
А, Б	Детская (пом. 7)	109
В, Г	Детская (пом. 7)	110
А, Б, В	Гардеробная (пом. 8)	111
Г	Гардеробная (пом. 8)	112
Б, В, Г	Кладовая (пом. 9)	113
А, В	Холл второго этажа (пом. 10)	114
Г	Холл второго этажа (пом. 10)	115
А, В, Г	Коридор второго этажа (пом. 11)	116
А, Б	Детская вторая (пом. 12)	117
В, Г	Детская вторая (пом. 12)	118
А	Санузел второго этажа (пом. 13)	119
Б	Санузел второго этажа (пом. 13)	120
В	Санузел второго этажа (пом. 13)	121
Г	Санузел второго этажа (пом. 13)	122
узел 1	Порог 15 мм: мокрая зона — жилое помещение	123
узел 2	Дверь скрытого монтажа в плоскости стены, плинтус	123
узел 3	Короб стояков К1-1 с люком и звукоизоляцией	123
…	ещё 2: см. ведомость рабочих чертежей, лист 2	

Изм.	Кол.уч	Лист	№ док.	Подп.	Дата
Разраб.		Кырлан А.С.			19.10.26
Пров.					
ГИП					
Н. контр.					
Утв.					

ГД-2026-012-АИ

Дом 120 м²

Общая площадь 147,36* м² · * размеры приняты, не замерены (реестр — л. 6, К-1)

Дизайн-проект интерьера

Стадия	Лист	Листов
РП	94	130

Схема расположения развёрток и узлов

М 1:50

Кырлан Александр Сергеевич

выпуск 19.10.2026 № 53e4f7ddae · стр. 100 из 160

Развёртка стены А. Гостиная-кухня (пом. 1), кухонный фронт

Гостиная-кухня (пом. 1) · вид изнутри помещения · размеры в мм, отметки в м

ПРЕДВАРИТЕЛЬНО · не для производства работ · открыто пунктов: 6 (реестр — л. 6)

Развёртка стены А

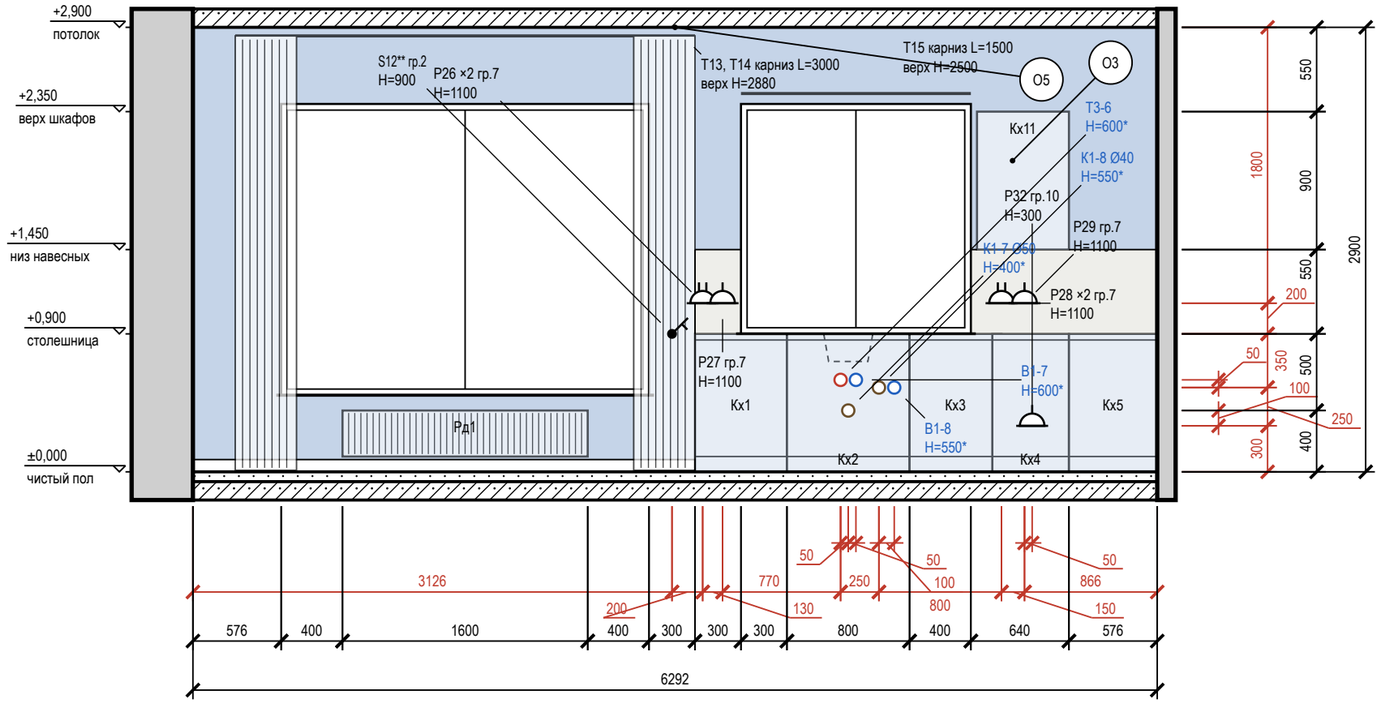

Условные обозначения

- розетка с заземляющим контактом; у знака — марка, ×N постов в рамке, гр. — группа щита, H — высота оси, мм
- выключатель одноклавишный
- вывод В1 (код — в ведомости привязок)
- вывод Т3 (код — в ведомости привязок)
- вывод К1 (код — в ведомости привязок)
- привязки точек и выводов от угла и от пола, мм
- мебель и приборы — фасад по расстановке (условно)
- карниз (шина) и шторы в собранном виде: марка Т, длина L, верх H
- окно: проём, рама, подоконник
- радиатор отопления; марка — по плану отопления
- стены и перекрытия в сечении
- плитка: сетка швов по формату, ▲ — ось старта
- окраска: тон — цвет по коду производителя (условно)
- О1 — марка отделки по реестру отделки альбома
- А — марка развёртки: буква стены, стрелка — взгляд

Схема развёрток (М 1:100)

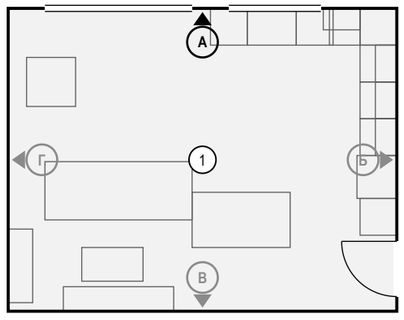

Ведомость отделки (на листе)

Марка	Поверхность	Материал, изделие	Цвет, код	Кол.
О2	фартук	керамогранит, 1200×600×9 мм, аналог: керамогранит под травертин, матовый, затирка CG2WA		0,8 м²
О3	акцентная стена	окраска, Farrow & Ball Modern Emulsion, матовая, подготовка Q3	NCS S 3050-R80B «Эгейский синий»	9,8 м²
О4	плинтус	плинтус МДФ, h 80 мм, аналог: плинтус МДФ под покраску 80×16	Tikkurila G503 «Calla»	3,3 м
О5	потолок	окраска, Tikkurila Anti-Reflex 2, глубокоматовая, подготовка Q3	Little Greene No. 222 «Loft White»	31,3 м²

Допущения и предложения на листе

Основа листа: взаимное расположение помещений, контур дома 9600 × 8000 и раскладка этажей подобраны проектировщиком под габариты помещений брифа; обмер и проект АР — задание (К-1); высота потолка 2900 мм — по брифу, не замерена; перекрытие 330 мм и отметка 2-го этажа +3,230 приняты; проект КР — задание (К-2); наружные стены 400 мм, перегородки 120 мм приняты (в брифе толщин нет) (К-1); разрешённая мощность 15 кВт принята по типовым ТУ для частного дома (К-4).

Знак «**» — предложение проектировщика, заказчиком не утверждено (согласовать с заказчиком): записи в реестре нет: S12 — светорегулятор добавлен разработчиком проекта.

См. лист открытых вопросов (лист 6, записи К-1, К-2, К-4).

Примечания

1. Развёртки — вид на стену изнутри помещения, по часовой стрелке; расположение — на схеме листа и на листе 94; размеры — в мм по чистовым поверхностям; отметки — в м от ±0,000; высоты H — от чистого пола помещения до оси изделия, у декора — до центра.
2. Красные цепочки — привязки электроточек и выводов: по горизонтали от угла чистовых стен, по вертикали от чистого пола, до оси изделия; звенья короче 3 мм на листе вынесены во второй ярус (ближняя к стене цепочка).
3. У знака электроточки: марка (Р — розетка, S — выключатель, Св — светильник, ЭВ — вывод кабеля), ×N — число постов в рамке, гр. — группа щита, H — высота оси от чистого пола, мм; группы по клавишам выключателя — на листе выключателей.
4. Схема мебели, приборов и декора не является технической документацией для производства мебели; габариты — по паспортам изделий.
5. Выводы ВК — коды и высоты по листу выводов сантехники; * — высота принята по типовой практике монтажа, окончательно — по паспорту прибора.
6. Карнизы (шины) — по ведомости текстиля декоратора; длина L и верх H — по развёртке, крепление — до окраски потолка.
7. Выводы кухонной техники — по утверждённому проекту кухни: привязки выводов даются от осей модулей гарнитура.

1000 мм · печать 1:1

Изм.	Кол.уч	Лист	№ док.	Подп.	Дата
Разраб.		Кырлан А.С.			19.10.26
Пров.					
ГИП					
Н. контр.					
Утв.					

ГД-2026-012-АИ

Дом 120 м²

Общая площадь 147,36* м² · * размеры приняты, не замерены (реестр — л. 6, К-1)

Дизайн-проект интерьера

Стадия	Лист	Листов
РП	95	130

Развёртка стены А. Гостиная-кухня (пом. 1), кухонный фронт

М 1:40

Кырлан Александр Сергеевич

выпуск 19.10.2026 № 53e4f7ddae · стр. 101 из 160

Развёртка стены Б. Гостиная-кухня (пом. 1), кухонный фронт

Гостиная-кухня (пом. 1) · вид изнутри помещения · размеры в мм, отметки в м

ПРЕДВАРИТЕЛЬНО · не для производства работ · открыто пунктов: 6 (реестр — л. 6)

Развёртка стены Б

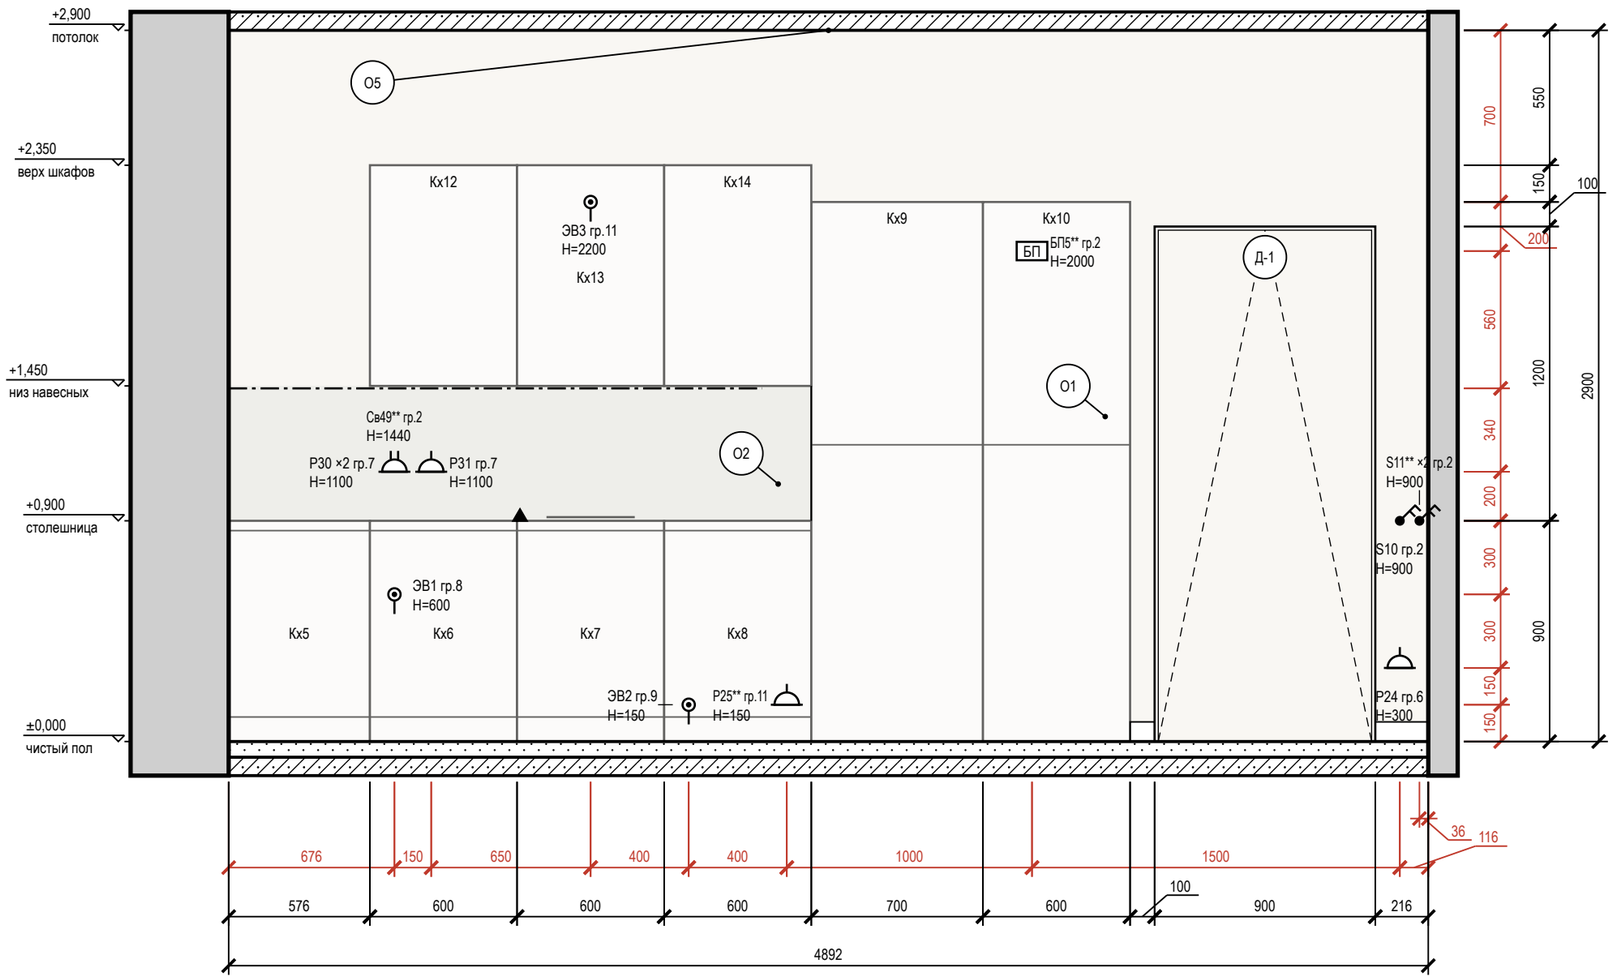

Схема развёрток (М 1:100)

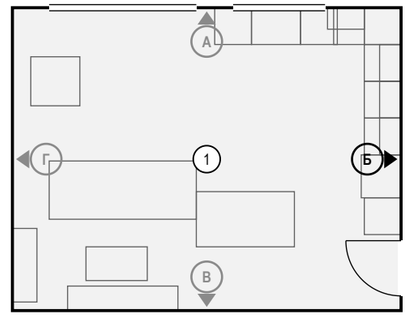

Условные обозначения

- розетка с заземляющим контактом; у знака — марка, ×N постов в рамке, гр. — группа щита, H — высота оси, мм
- вывод кабеля для подключения прибора (без розетки), марка ЭВ
- выключатель одноклавишный
- выключатель двухклавишный (флажков — по числу клавиш)
- светодиодная лента в профиле / в карнизе короба
- БП — блок питания LED, с доступом (люк от 100×100 мм)
- привязки точек и выводов от угла и от пола, мм
- мебель и приборы — фасад по расстановке (условно)
- дверь скрытого монтажа: полотно в плоскости стены (узел — на листе узлов)
- стены и перекрытия в сечении
- плитка: сетка швов по формату, ▲ — ось старта
- окраска: тон — цвет по коду производителя (условно)
- О1 — марка отделки по реестру отделки альбома
- А — марка развёртки: буква стены, стрелка — взгляд

Допущения и предложения на листе

Основа листа: взаимное расположение помещений, контур дома 9600 × 8000 и раскладка этажей подобраны проектировщиком под габариты помещений брифа; обмер и проект АР — задание (К-1); высота потолка 2900 мм — по брифу, не замерена; перекрытие 330 мм и отметка 2-го этажа +3,230 приняты; проект КР — задание (К-2); наружные стены 400 мм, перегородки 120 мм приняты (в брифе толщин нет) (К-1); разрешённая мощность 15 кВт принята по типовым ТУ для частного дома (К-4).

Знак «**» — предложение проектировщика, заказчиком не утверждено (согласовать с заказчиком): записи в реестре нет: S11 — светорегулятор добавлен разработчиком проекта; Р25 — высота 2000 мм выше нормы 1 м (ПУЭ 6.6.30) по назначению: питание встроенного холодильника М6, розетка над нишей за съёмной панелью; Св49, БП5 — диммируемость добавлена разработчиком проекта под светорегуляторы S11 и S12.

См. лист открытых вопросов (лист 6, записи К-1, К-2, К-4).

Примечания

1. Развёртки — вид на стену изнутри помещения, по часовой стрелке; расположение — на схеме листа и на листе 94; размеры — в мм по чистовым поверхностям; отметки — в м от ±0,000; высоты H — от чистого пола помещения до оси изделия, у декора — до центра.
2. Красные цепочки — привязки электроточек и выводов: по горизонтали от угла чистовых стен, по вертикали от чистого пола, до оси изделия; звенья короче 3 мм на листе вынесены во второй ярус (ближняя к стене цепочка).
3. У знака электроточки: марка (Р — розетка, S — выключатель, Св — светильник, ЭВ — вывод кабеля), ×N — число постов в рамке, гр. — группа щита, H — высота оси от чистого пола, мм; группы по клавишам выключателя — на листе выключателей.
4. Схема мебели, приборов и декора не является технической документацией для производства мебели; габариты — по паспортам изделий.
5. Двери скрытого монтажа — полотно в плоскости стены, отделка стены по полотну, плинтус прерывается у короба (узел — на листе узлов).
6. Выводы кухонной техники — по утверждённому проекту кухни: привязки выводов даются от осей модулей гарнитура.

1000 мм · печать 1:1

Изм.	Кол.уч	Лист	№ док.	Подп.	Дата
Разраб.		Кырлан А.С.			19.10.26
Пров.					
ГИП					
Н. контр.					
Утв.					

ГД-2026-012-АИ

Дом 120 м²

Общая площадь 147,36* м² · * размеры приняты, не замерены (реестр — л. 6, К-1)

Дизайн-проект интерьера	Стадия	Лист	Листов
	РП	96	130

Развёртка стены Б. Гостиная-кухня (пом. 1), кухонный фронт

М 1:25

Кырлан Александр Сергеевич

выпуск 19.10.2026 № 53e4f7ddae · стр. 102 из 160

Развёртка стены В. Гостиная-кухня (пом. 1)

Гостиная-кухня (пом. 1) · вид изнутри помещения · размеры в мм, отметки в м

ПРЕДВАРИТЕЛЬНО · не для производства работ · открыто пунктов: 6 (реестр — л. 6)

Развёртка стены В

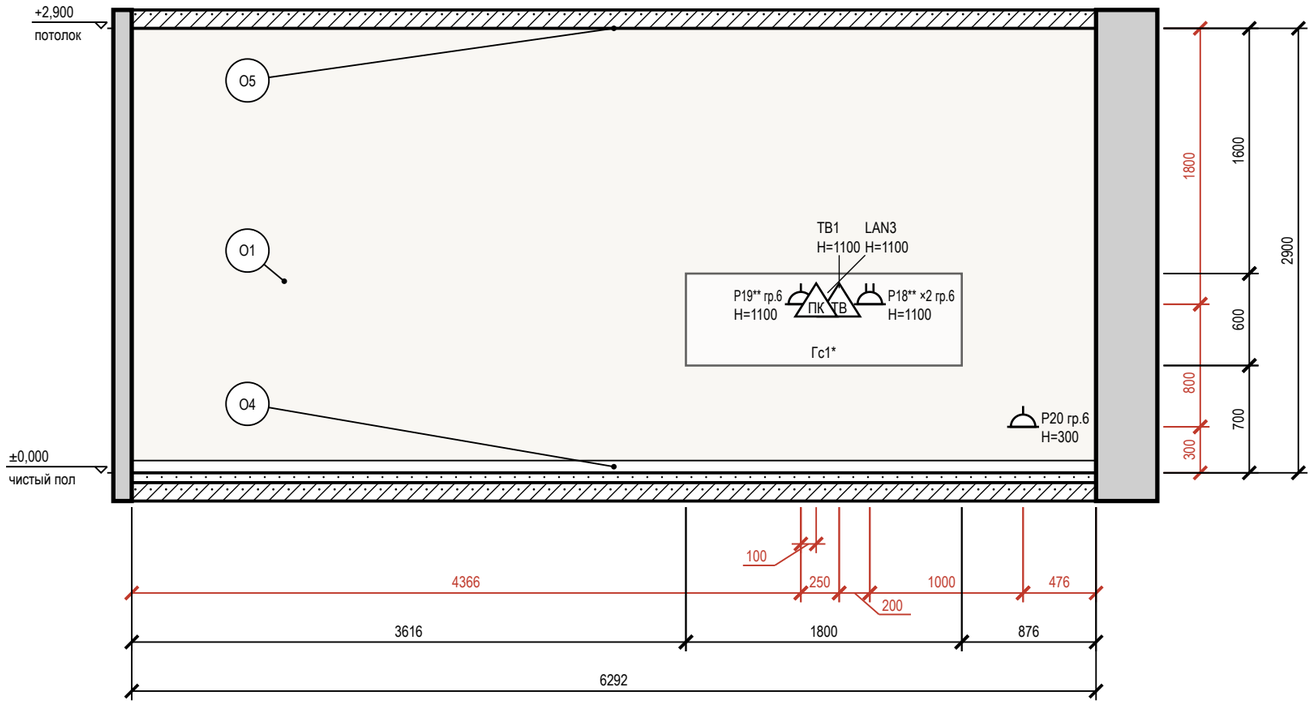

Схема развёрток (М 1:100)

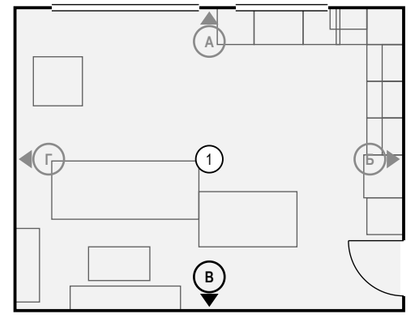

Условные обозначения

- розетка с заземляющим контактом; у знака — марка, ×N постов в рамке, гр. — группа щита, Н — высота оси, мм
- ПК — розетка компьютерная RJ45
- ТВ — розетка телевизионная
- привязки точек и выводов от угла и от пола, мм
- мебель и приборы — фасад по расстановке (условно)
- стены и перекрытия в сечении
- окраска: тон — цвет по коду производителя (условно)
- О1 — марка отделки по реестру отделки альбома
- А — марка развёртки: буква стены, стрелка — взгляд

Ведомость отделки (на листе)

Марка	Поверхность	Материал, изделие	Цвет, код	Кол.
О1	стены	окраска, Farrow & Ball Modern Emulsion, матовая, подготовка Q3	Tikkurila G503 «Calla»	18,2 м²
О4	плинтус	плинтус МДФ, h 80 мм, аналог: плинтус МДФ под покраску 80×16	Tikkurila G503 «Calla»	6,3 м
О5	потолок	окраска, Tikkurila Anti-Reflex 2, глубокоматовая, подготовка Q3	Little Greene No. 222 «Loft White»	31,3 м²

Допущения и предложения на листе

Основа листа: взаимное расположение помещений, контур дома 9600 × 8000 и раскладка этажей подобраны проектировщиком под габариты помещений брифа; обмер и проект АР — задание (К-1); высота потолка 2900 мм — по брифу, не замерена; перекрытие 330 мм и отметка 2-го этажа +3,230 приняты; проект КР — задание (К-2); наружные стены 400 мм, перегородки 120 мм приняты (в брифе толщин нет) (К-1); разрешённая мощность 15 кВт принята по типовым ТУ для частного дома (К-4).

Знак «**» — предложение проектировщика, заказчиком не утверждено (согласовать с заказчиком): записи в реестре нет: Р18 — высота 1100 мм выше нормы 1 м (ПУЭ 6.6.30) по назначению: питание ТВ, в одной зоне с выводами TB1 и LAN3; Р19 — высота 1100 мм выше нормы 1 м (ПУЭ 6.6.30) по назначению: питание приставки ТВ, в одной зоне с выводами TB1 и LAN3.

См. лист открытых вопросов (лист 6, записи К-1, К-2, К-4).

Примечания

1. Развёртки — вид на стену изнутри помещения, по часовой стрелке; расположение — на схеме листа и на листе 94; размеры — в мм по чистовым поверхностям; отметки — в м от ±0,000; высоты Н — от чистого пола помещения до оси изделия, у декора — до центра.
2. Красные цепочки — привязки электроточек и выводов: по горизонтали от угла чистовых стен, по вертикали от чистого пола, до оси изделия; звенья короче 3 мм на листе вынесены во второй ярус (ближняя к стене цепочка).
3. У знака электроточки: марка (Р — розетка, S — выключатель, Св — светильник, ЭВ — вывод кабеля), ×N — число постов в рамке, гр. — группа щита, Н — высота оси от чистого пола, мм; группы по клавишам выключателя — на листе выключателей.
4. Схема мебели, приборов и декора не является технической документацией для производства мебели; габариты — по паспортам изделий (* — высота не задана в проекте, показана по типовому изделию).

1000 мм · печать 1:1

Изм.	Кол.уч	Лист	№ док.	Подп.	Дата
Разраб.		Кырлан А.С.			19.10.26
Пров.					
ГИП					
Н. контр.					
Утв.					

ГД-2026-012-АИ

Дом 120 м²

Общая площадь 147,36* м² · * размеры приняты, не замерены (реестр — л. 6, К-1)

Дизайн-проект интерьера

Стадия	Лист	Листов
РП	97	130

Развёртка стены В. Гостиная-кухня (пом. 1)

М 1:40

Кырлан Александр Сергеевич

выпуск 19.10.2026 № 53e4f7ddae · стр. 103 из 160

Развёртка стены Г. Гостиная-кухня (пом. 1)

Гостиная-кухня (пом. 1) · вид изнутри помещения · размеры в мм, отметки в м

ПРЕДВАРИТЕЛЬНО · не для производства работ · открыто пунктов: 6 (реестр — л. 6)

Развёртка стены Г

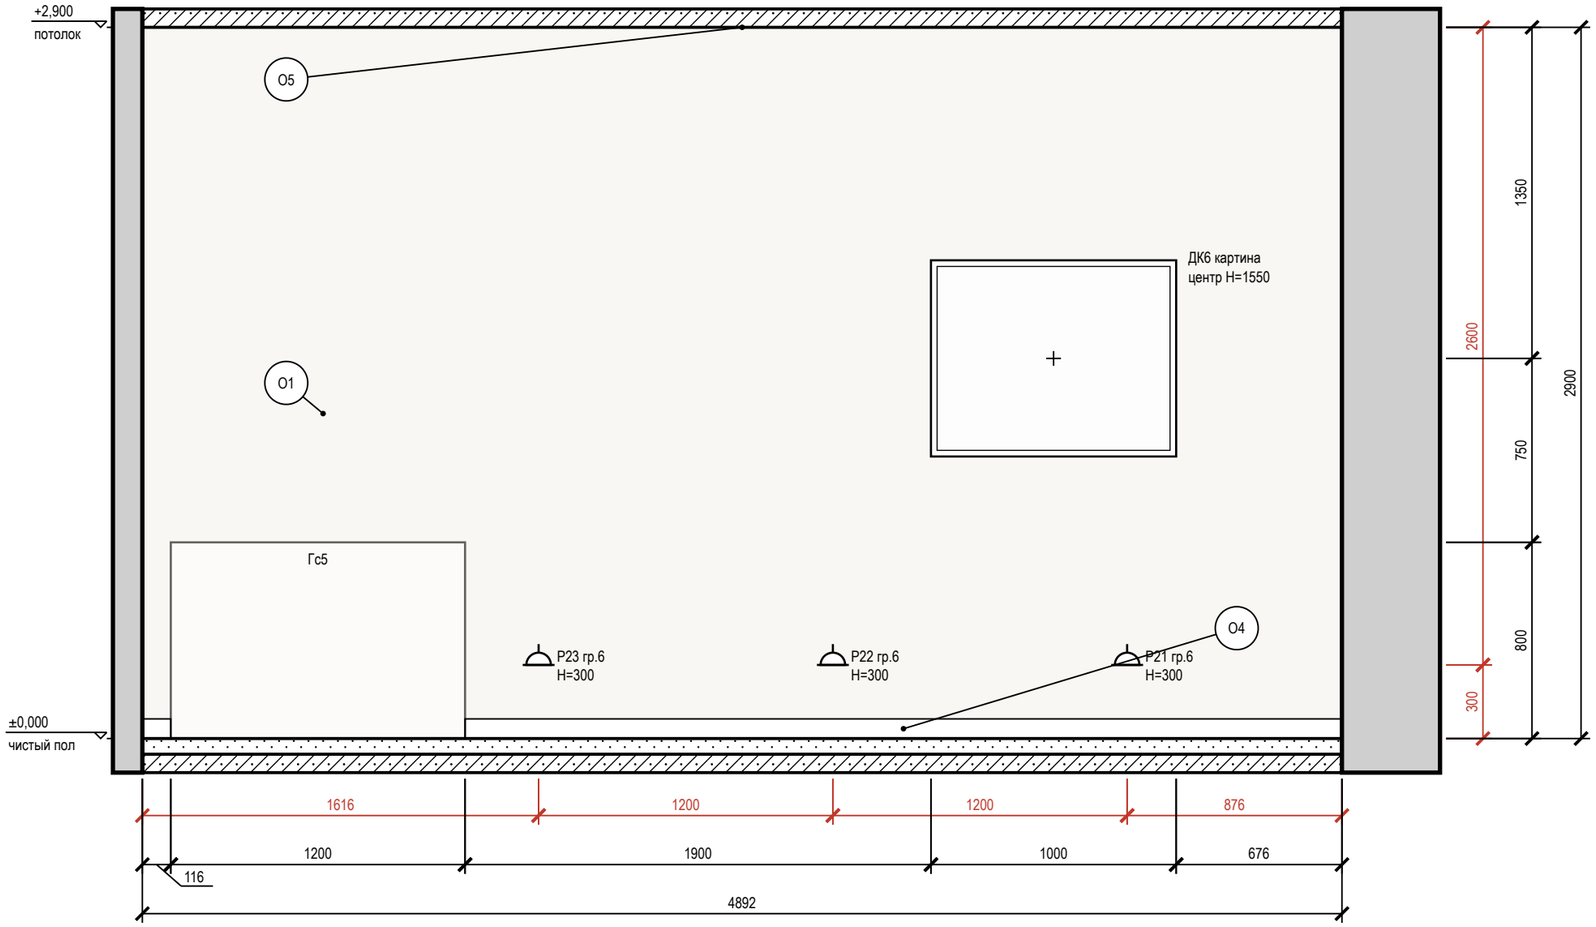

Схема развёрток (М 1:100)

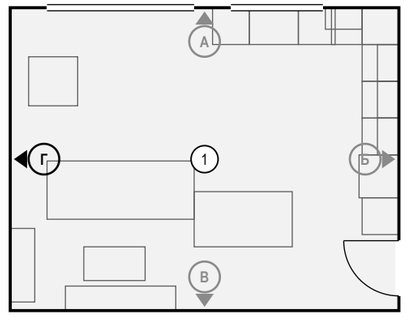

Условные обозначения

- розетка с заземляющим контактом; у знака — марка, ×N постов в рамке, гр. — группа щита, Н — высота оси, мм
- привязки точек и выводов от угла и от пола, мм
- мебель и приборы — фасад по расстановке (условно)
- картина (декор): марка Д, крест — центр, Н — высота центра, мм
- стены и перекрытия в сечении
- окраска: тон — цвет по коду производителя (условно)
- О1 — марка отделки по реестру отделки альбома
- А — марка развёртки: буква стены, стрелка — взгляд

Ведомость отделки (на листе)

Марка	Поверхность	Материал, изделие	Цвет, код	Кол.
О1	стены	окраска, Farrow & Ball Modern Emulsion, матовая, подготовка Q3	Tikkurila G503 «Calla»	14,2 м²
О4	плинтус	плинтус МДФ, h 80 мм, аналог: плинтус МДФ под покраску 80×16	Tikkurila G503 «Calla»	3,7 м
О5	потолок	окраска, Tikkurila Anti-Reflex 2, глубокоматовая, подготовка Q3	Little Greene No. 222 «Loft White»	31,3 м²

Допущения и предложения на листе

Основа листа: взаимное расположение помещений, контур дома 9600 × 8000 и раскладка этажей подобраны проектировщиком под габариты помещений брифа; обмер и проект АР — задание (К-1); высота потолка 2900 мм — по брифу, не замерена; перекрытие 330 мм и отметка 2-го этажа +3,230 приняты; проект КР — задание (К-2); наружные стены 400 мм, перегородки 120 мм приняты (в брифе толщин нет) (К-1); разрешённая мощность 15 кВт принята по типовым ТУ для частного дома (К-4).

См. лист открытых вопросов (лист 6, записи К-1, К-2, К-4).

Примечания

1. Развёртки — вид на стену изнутри помещения, по часовой стрелке; расположение — на схеме листа и на листе 94; размеры — в мм по чистовым поверхностям; отметки — в м от ±0,000; высоты Н — от чистого пола помещения до оси изделия, у декора — до центра.
2. Красные цепочки — привязки электроточек и выводов: по горизонтали от угла чистовых стен, по вертикали от чистого пола, до оси изделия; звенья короче 3 мм на листе вынесены во второй ярус (ближняя к стене цепочка).
3. У знака электроточки: марка (Р — розетка, S — выключатель, Св — светильник, ЭВ — вывод кабеля), ×N — число постов в рамке, гр. — группа щита, Н — высота оси от чистого пола, мм; группы по клавишам выключателя — на листе выключателей.
4. Схема мебели, приборов и декора не является технической документацией для производства мебели; габариты — по паспортам изделий.
5. Картины и зеркала крепить к основанию по паспорту изделия (закладные и анкеры — в перечне скрытых работ); крест — ось центра предмета.

1000 мм · печать 1:1

Изм.	Кол.уч	Лист	№ док.	Подп.	Дата
Разраб.		Кырлан А.С.			19.10.26
Пров.					
ГИП					
Н. контр.					
Утв.					

ГД-2026-012-АИ

Дом 120 м²

Общая площадь 147,36* м² · * размеры приняты, не замерены (реестр — л. 6, К-1)

Дизайн-проект интерьера

Стадия	Лист	Листов
РП	98	130

Развёртка стены Г. Гостиная-кухня (пом. 1)

М 1:25

Кырлан Александр Сергеевич

выпуск 19.10.2026 № 53e4f7ddae · стр. 104 из 160

Развёртки стен А, В. Холл с лестницей (пом. 2)

Холл с лестницей (пом. 2) · вид изнутри помещения · размеры в мм, отметки в м

ПРЕДВАРИТЕЛЬНО · не для производства работ · открыто пунктов: 6 (реестр — л. 6)

Развёртка стены А

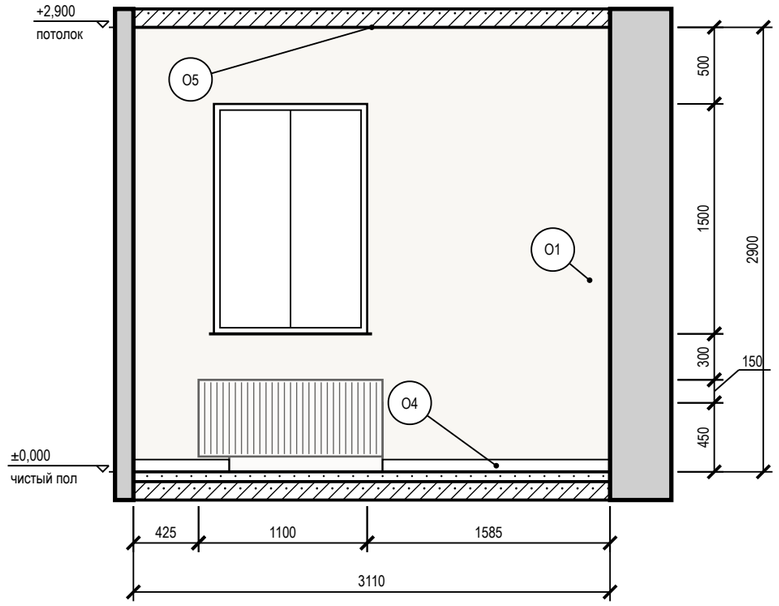

Развёртка стены В

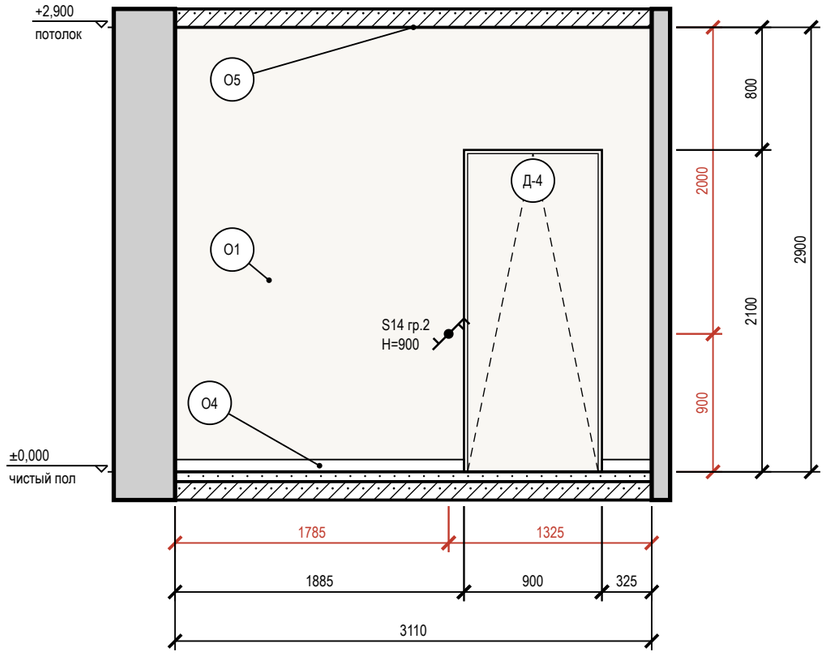

Условные обозначения

- выключатель одноклавишный
- выключатель двухклавишный (флажков — по числу клавиш)
- выключатель с проходной или перекрёстной клавишей (обратный флажок); тип клавиши — в подписи
- привязки точек и выводов от угла и от пола, мм
- мебель и приборы — фасад по расстановке (условно)
- дверь скрытого монтажа: полотно в плоскости стены (узел — на листе узлов)
- окно: проём, рама, подоконник
- радиатор отопления; марка — по плану отопления
- стены и перекрытия в сечении
- окраска: тон — цвет по коду производителя (условно)
- О1 — марка отделки по реестру отделки альбома
- А — марка развёртки: буква стены, стрелка — взгляд

Схема развёрток (М 1:100)

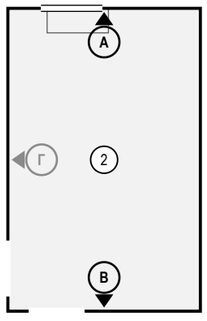

Ведомость отделки (на листе)

Марка	Поверхность	Материал, изделие	Цвет, код	Кол.
О1	стены	окраска, Farrow & Ball Modern Emulsion, матовая, подготовка Q3	Tikkurila G503 «Calla»	14,6 м²
О4	плинтус	плинтус МДФ, h 80 мм, аналог: плинтус МДФ под покраску 80×16	Tikkurila G503 «Calla»	4,3 м
О5	потолок	окраска, Tikkurila Anti-Reflex 2, глубокоматовая, подготовка Q3	Little Greene No. 222 «Loft White»	15,5 м²

Допущения и предложения на листе

Основа листа: взаимное расположение помещений, контур дома 9600 × 8000 и раскладка этажей подобраны проектировщиком под габариты помещений брифа; обмер и проект АР — задание (К-1); высота потолка 2900 мм — по брифу, не замерена; перекрытие 330 мм и отметка 2-го этажа +3,230 приняты; проект КР — задание (К-2); наружные стены 400 мм, перегородки 120 мм приняты (в брифе толщин нет) (К-1); разрешённая мощность 15 кВт принята по типовым ТУ для частного дома (К-4).
См. лист открытых вопросов (лист 6, записи К-1, К-2, К-4).

Примечания

1. Развёртки — вид на стену изнутри помещения, по часовой стрелке; расположение — на схеме листа и на листе 94; размеры — в мм по чистовым поверхностям; отметки — в м от ±0,000; высоты Н — от чистого пола помещения до оси изделия, у декора — до центра.
2. Красные цепочки — привязки электроточек и выводов: по горизонтали от угла чистовых стен, по вертикали от чистого пола, до оси изделия; звенья короче 3 мм на листе вынесены во второй ярус (ближняя к стене цепочка).
3. У знака электроточки: марка (Р — розетка, S — выключатель, Св — светильник, ЭВ — вывод кабеля), ×N — число постов в рамке, гр. — группа щита, Н — высота оси от чистого пола, мм; группы по клавишам выключателя — на листе выключателей.
4. Схема мебели, приборов и декора не является технической документацией для производства мебели; габариты — по паспортам изделий.
5. Двери скрытого монтажа — полотно в плоскости стены, отделка стены по полотну, плинтус прерывается у короба (узел — на листе узлов).

1000 мм · печать 1:1

Изм.	Кол.уч	Лист	№ док.	Подп.	Дата
Разраб.		Кырлан А.С.			19.10.26
Пров.					
ГИП					
Н. контр.					
Утв.					

ГД-2026-012-АИ

Дом 120 м²

Общая площадь 147,36* м² · * размеры приняты, не замерены (реестр — л. 6, К-1)

Дизайн-проект интерьера

Стадия	Лист	Листов
РП	99	130

Развёртки стен А, В. Холл с лестницей (пом. 2)

М 1:40

Кырлан Александр Сергеевич

Развёртка стены Г. Холл с лестницей (пом. 2)

Холл с лестницей (пом. 2) · вид изнутри помещения · размеры в мм, отметки в м

ПРЕДВАРИТЕЛЬНО · не для производства работ · открыто пунктов: 6 (реестр — л. 6)

Развёртка стены Г

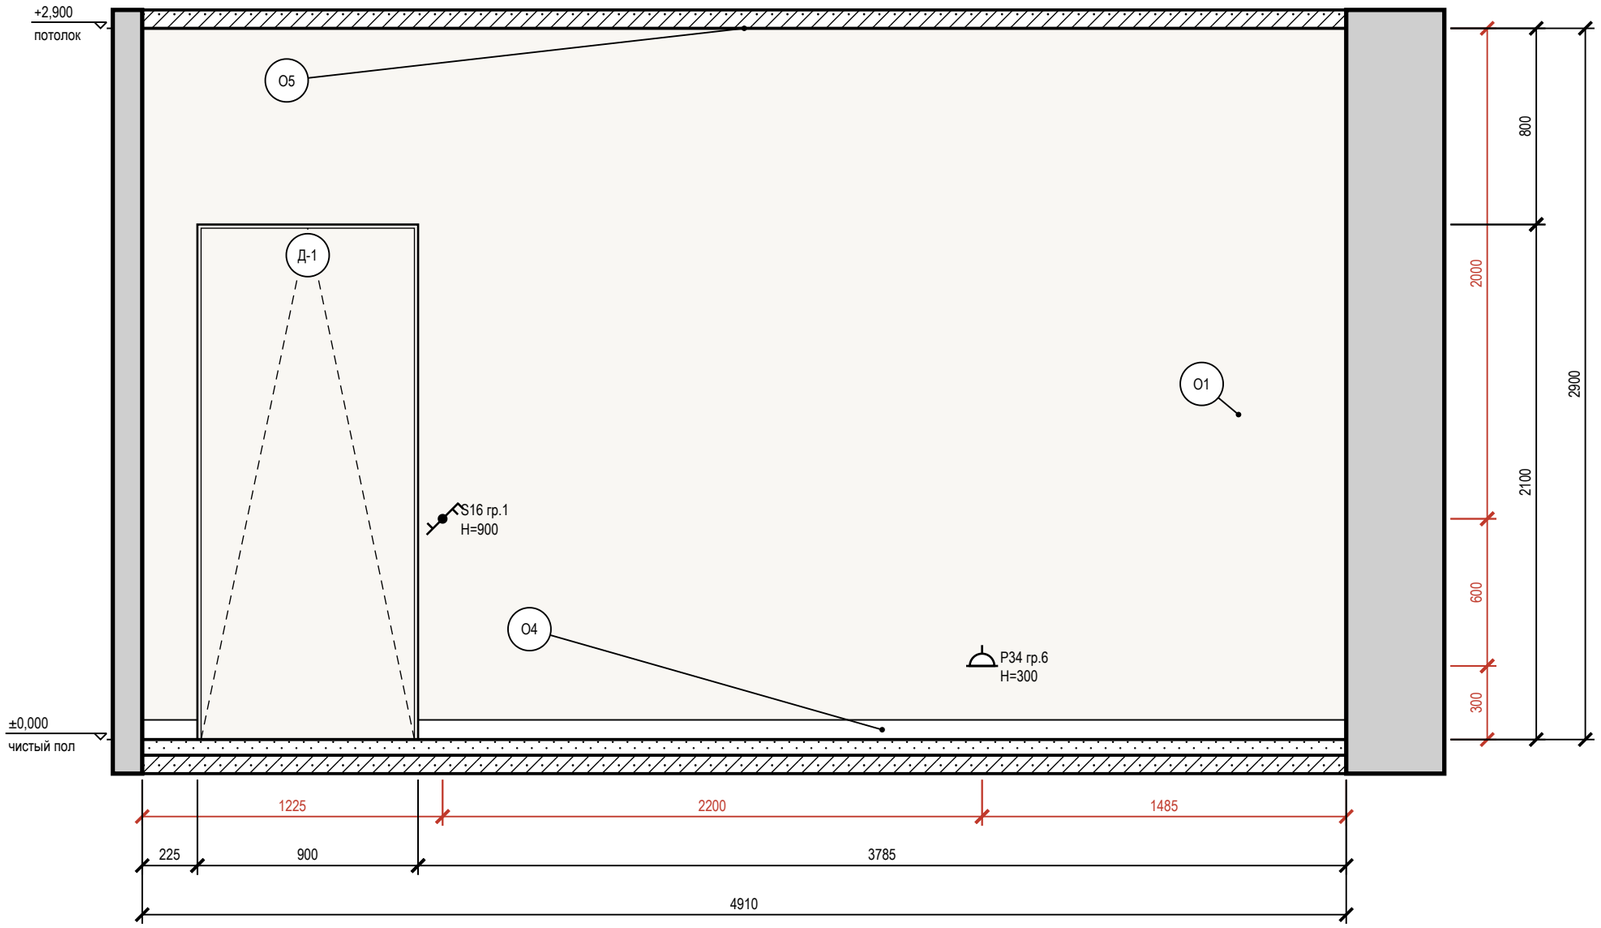

Схема развёрток (М 1:100)

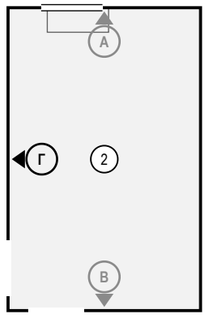

Условные обозначения

- розетка с заземляющим контактом; у знака — марка, ×N постов в рамке, гр. — группа щита, H — высота оси, мм
- выключатель одноклавишный
- выключатель двухклавишный (флажков — по числу клавиш)
- выключатель с проходной или перекрёстной клавишей (обратный флажок); тип клавиши — в подписи
- привязки точек и выводов от угла и от пола, мм
- мебель и приборы — фасад по расстановке (условно)
- дверь скрытого монтажа: полотно в плоскости стены (узел — на листе узлов)
- стены и перекрытия в сечении
- окраска: тон — цвет по коду производителя (условно)
- О1 — марка отделки по реестру отделки альбома
- А — марка развёртки: буква стены, стрелка — взгляд

Ведомость отделки (на листе)

Марка	Поверхность	Материал, изделие	Цвет, код	Кол.
О1	стены	окраска, Farrow & Ball Modern Emulsion, матовая, подготовка Q3	Tikkurila G503 «Calla»	12,3 м²
О4	плинтус	плинтус МДФ, h 80 мм, аналог: плинтус МДФ под покраску 80×16	Tikkurila G503 «Calla»	4 м
О5	потолок	окраска, Tikkurila Anti-Reflex 2, глубокоматовая, подготовка Q3	Little Greene No. 222 «Loft White»	15,5 м²

Допущения и предложения на листе

Основа листа: взаимное расположение помещений, контур дома 9600 × 8000 и раскладка этажей подобраны проектировщиком под габариты помещений брифа; обмер и проект АР — задание (К-1); высота потолка 2900 мм — по брифу, не замерена; перекрытие 330 мм и отметка 2-го этажа +3,230 приняты; проект КР — задание (К-2); наружные стены 400 мм, перегородки 120 мм приняты (в брифе толщин нет) (К-1); разрешённая мощность 15 кВт принята по типовым ТУ для частного дома (К-4).
См. лист открытых вопросов (лист 6, записи К-1, К-2, К-4).

Примечания

1. Развёртки — вид на стену изнутри помещения, по часовой стрелке; расположение — на схеме листа и на листе 94; размеры — в мм по чистовым поверхностям; отметки — в м от ±0,000; высоты H — от чистого пола помещения до оси изделия, у декора — до центра.
2. Красные цепочки — привязки электроточек и выводов: по горизонтали от угла чистовых стен, по вертикали от чистого пола, до оси изделия; звенья короче 3 мм на листе вынесены во второй ярус (ближняя к стене цепочка).
3. У знака электроточки: марка (Р — розетка, S — выключатель, Св — светильник, ЭВ — вывод кабеля), ×N — число постов в рамке, гр. — группа щита, H — высота оси от чистого пола, мм; группы по клавишам выключателя — на листе выключателей.
4. Схема мебели, приборов и декора не является технической документацией для производства мебели; габариты — по паспортам изделий.
5. Двери скрытого монтажа — полотно в плоскости стены, отделка стены по полотну, плинтус прерывается у короба (узел — на листе узлов).

1000 мм · печать 1:1

Изм.	Кол.уч	Лист	№ док.	Подп.	Дата
Разраб.		Кырлан А.С.			19.10.26
Пров.					
ГИП					
Н. контр.					
Утв.					

ГД-2026-012-АИ

Дом 120 м²

Общая площадь 147,36* м² · * размеры приняты, не замерены (реестр — л. 6, К-1)

Дизайн-проект интерьера

Стадия	Лист	Листов
РП	100	130

Развёртка стены Г. Холл с лестницей (пом. 2)

М 1:25

Кырлан Александр Сергеевич

выпуск 19.10.2026 № 53e4f7ddae · стр. 106 из 160

Развёртки стен А, Б. Кабинет (пом. 3)

Кабинет (пом. 3) · вид изнутри помещения · размеры в мм, отметки в м

ПРЕДВАРИТЕЛЬНО · не для производства работ · открыто пунктов: 6 (реестр — л. 6)

Развёртка стены А

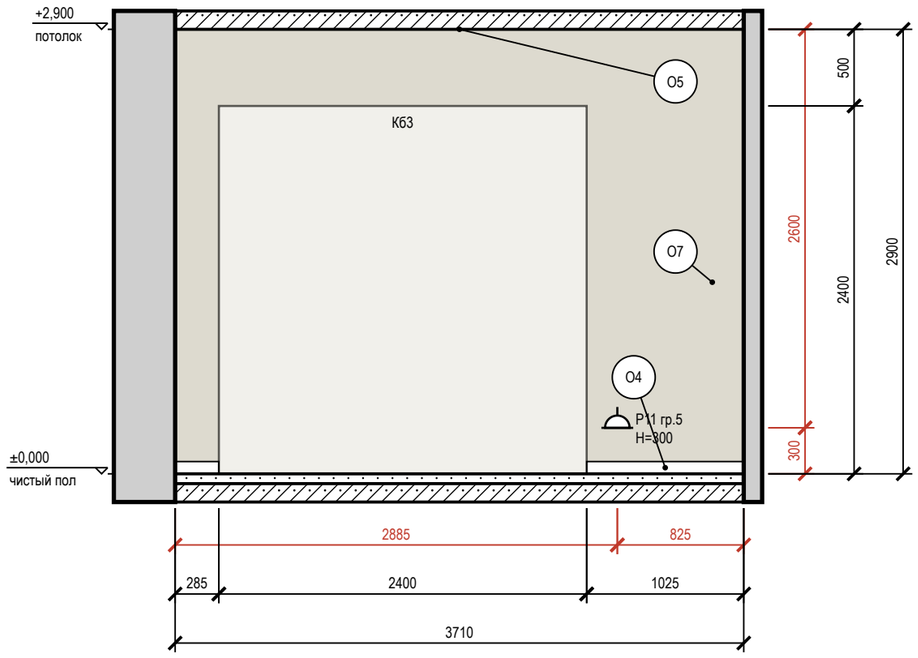

Развёртка стены Б

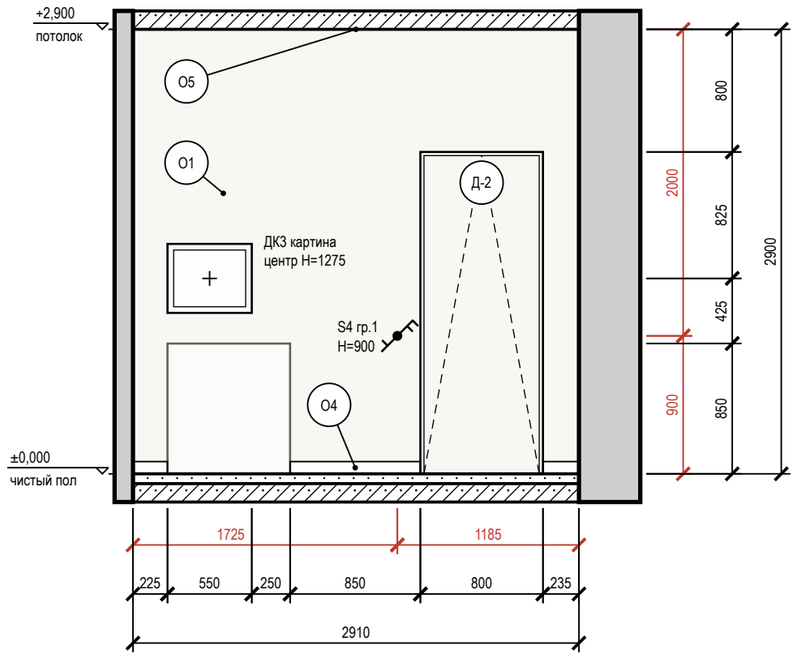

Условные обозначения

- розетка с заземляющим контактом; у знака — марка, ×N постов в рамке, гр. — группа щита, Н — высота оси, мм
- выключатель одноклавишный
- выключатель двухклавишный (флажков — по числу клавиш)
- выключатель с проходной или перекрёстной клавишей (обратный флажок); тип клавиши — в подписи
- привязки точек и выводов от угла и от пола, мм
- мебель и приборы — фасад по расстановке (условно)
- картина (декор): марка Д, крест — центр, Н — высота центра, мм
- дверь скрытого монтажа: полотно в плоскости стены (узел — на листе узлов)
- стены и перекрытия в сечении
- окраска: тон — цвет по коду производителя (условно)
- О1 — марка отделки по реестру отделки альбома
- А — марка развёртки: буква стены, стрелка — взгляд

Схема развёрток (М 1:100)

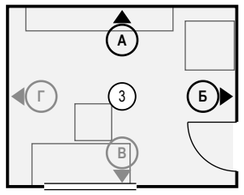

Ведомость отделки (на листе)

Марка	Поверхность	Материал, изделие	Цвет, код	Кол.
О1	стены	окраска, Farrow & Ball Modern Emulsion, матовая, подготовка Q3	Tikkurila G503 «Calla»	6,8 м²
О4	плинтус	плинтус МДФ, h 80 мм, аналог: плинтус МДФ под покраску 80×16	Tikkurila G503 «Calla»	2,6 м
О5	потолок	окраска, Tikkurila Anti-Reflex 2, глубокоматовая, подготовка Q3	Little Greene No. 222 «Loft White»	11 м²
О7	акцентная стена	окраска, Farrow & Ball Modern Emulsion, матовая, подготовка Q3	NCS S 5020-G90Y «Олива»	10,8 м²

Допущения и предложения на листе

Основа листа: взаимное расположение помещений, контур дома 9600 × 8000 и раскладка этажей подобраны проектировщиком под габариты помещений брифа; обмер и проект АР — задание (К-1); высота потолка 2900 мм — по брифу, не замерена; перекрытие 330 мм и отметка 2-го этажа +3,230 приняты; проект КР — задание (К-2); наружные стены 400 мм, перегородки 120 мм приняты (в брифе толщин нет) (К-1); разрешённая мощность 15 кВт принята по типовым ТУ для частного дома (К-4).
См. лист открытых вопросов (лист 6, записи К-1, К-2, К-4).

Примечания

1. Развёртки — вид на стену изнутри помещения, по часовой стрелке; расположение — на схеме листа и на листе 94; размеры — в мм по чистовым поверхностям; отметки — в м от ±0,000; высоты Н — от чистого пола помещения до оси изделия, у декора — до центра.
2. Красные цепочки — привязки электроточек и выводов: по горизонтали от угла чистовых стен, по вертикали от чистого пола, до оси изделия; звенья короче 3 мм на листе вынесены во второй ярус (ближняя к стене цепочка).
3. У знака электроточки: марка (Р — розетка, S — выключатель, Св — светильник, ЭВ — вывод кабеля), ×N — число постов в рамке, гр. — группа щита, Н — высота оси от чистого пола, мм; группы по клавишам выключателя — на листе выключателей.
4. Схема мебели, приборов и декора не является технической документацией для производства мебели; габариты — по паспортам изделий.
5. Картины и зеркала крепить к основанию по паспорту изделия (закладные и анкеры — в перечне скрытых работ); крест — ось центра предмета.
6. Двери скрытого монтажа — полотно в плоскости стены, отделка стены по полотну, плинтус прерывается у короба (узел — на листе узлов).

1000 мм · печать 1:1

Изм.	Кол.уч	Лист	№ док.	Подп.	Дата
Разраб.		Кырлан А.С.			19.10.26
Пров.					
ГИП					
Н. контр.					
Утв.					

ГД-2026-012-АИ

Дом 120 м²

Общая площадь 147,36* м² · * размеры приняты, не замерены (реестр — л. 6, К-1)

Дизайн-проект интерьера

Стадия	Лист	Листов
РП	101	130

Развёртки стен А, Б. Кабинет (пом. 3)

М 1:40

Кырлан Александр Сергеевич

выпуск 19.10.2026 № 536a1f7ddae · стр. 107 из 160

Развёртки стен В, Г. Кабинет (пом. 3)

Кабинет (пом. 3) · вид изнутри помещения · размеры в мм, отметки в м

ПРЕДВАРИТЕЛЬНО · не для производства работ · открыто пунктов: 6 (реестр — л. 6)

Развёртка стены В

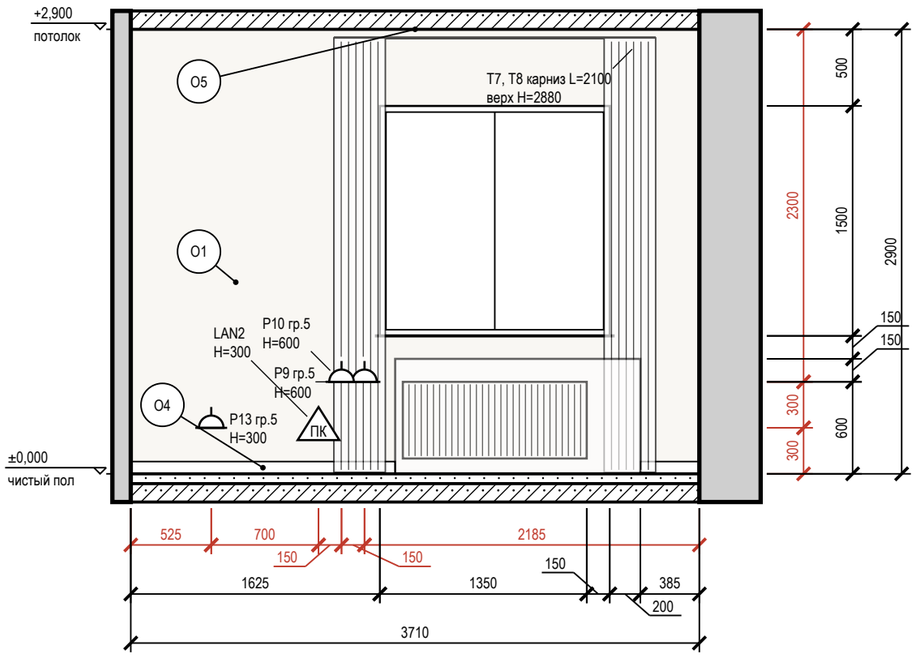

Развёртка стены Г

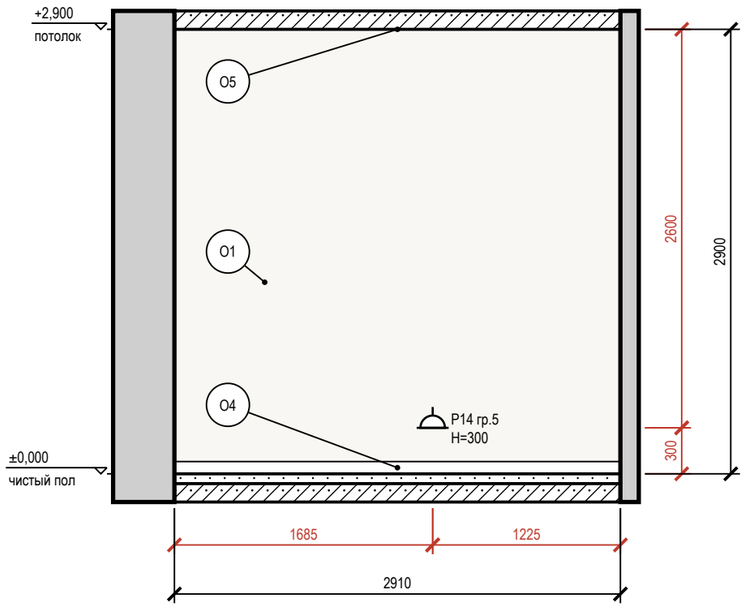

Условные обозначения

- розетка с заземляющим контактом; у знака — марка, ×N постов в рамке, гр. — группа щита, H — высота оси, мм
- ПК — розетка компьютерная RJ45
- привязки точек и выводов от угла и от пола, мм
- мебель и приборы — фасад по расстановке (условно)
- карниз (шина) и шторы в собранном виде: марка T, длина L, верх H
- окно: проём, рама, подоконник
- радиатор отопления; марка — по плану отопления
- стены и перекрытия в сечении
- окраска: тон — цвет по коду производителя (условно)
- О1 — марка отделки по реестру отделки альбома
- A — марка развёртки: буква стены, стрелка — взгляд

Схема развёрток (М 1:100)

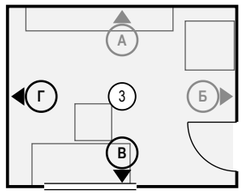

Ведомость отделки (на листе)

Марка	Поверхность	Материал, изделие	Цвет, код	Кол.
О1	стены	окраска, Farrow & Ball Modern Emulsion, матовая, подготовка Q3	Tikkurila G503 «Calla»	16,9 м²
О4	плинтус	плинтус МДФ, h 80 мм, аналог: плинтус МДФ под покраску 80×16	Tikkurila G503 «Calla»	5 м
О5	потолок	окраска, Tikkurila Anti-Reflex 2, глубокоматовая, подготовка Q3	Little Greene No. 222 «Loft White»	11 м²

Допущения и предложения на листе

Основа листа: взаимное расположение помещений, контур дома 9600 × 8000 и раскладка этажей подобраны проектировщиком под габариты помещений брифа; обмер и проект АР — задание (К-1); высота потолка 2900 мм — по брифу, не замерена; перекрытие 330 мм и отметка 2-го этажа +3,230 приняты; проект КР — задание (К-2); наружные стены 400 мм, перегородки 120 мм приняты (в брифе толщин нет) (К-1); разрешённая мощность 15 кВт принята по типовым ТУ для частного дома (К-4).
См. лист открытых вопросов (лист 6, записи К-1, К-2, К-4).

Примечания

1. Развёртки — вид на стену изнутри помещения, по часовой стрелке; расположение — на схеме листа и на листе 94; размеры — в мм по чистовым поверхностям; отметки — в м от ±0,000; высоты H — от чистого пола помещения до оси изделия, у декора — до центра.
2. Красные цепочки — привязки электроточек и выводов: по горизонтали от угла чистовых стен, по вертикали от чистого пола, до оси изделия; звенья короче 3 мм на листе вынесены во второй ярус (ближняя к стене цепочка).
3. У знака электроточки: марка (Р — розетка, S — выключатель, Св — светильник, ЭВ — вывод кабеля), ×N — число постов в рамке, гр. — группа щита, H — высота оси от чистого пола, мм; группы по клавишам выключателя — на листе выключателей.
4. Схема мебели, приборов и декора не является технической документацией для производства мебели; габариты — по паспортам изделий.
5. Карнизы (шины) — по ведомости текстиля декоратора; длина L и верх H — по развёртке, крепление — до окраски потолка.
6. Линии узора (швы плитки, складки штор, рёбра радиаторов) прерываются у знаков и выносок — просвет между линиями не менее 0,7 мм.

1000 мм · печать 1:1

Изм.	Кол.уч	Лист	№ док.	Подп.	Дата
Разраб.		Кырлан А.С.			19.10.26
Пров.					
ГИП					
Н. контр.					
Утв.					

ГД-2026-012-АИ

Дом 120 м²

Общая площадь 147,36* м² · * размеры приняты, не замерены (реестр — л. 6, К-1)

Дизайн-проект интерьера

Стадия	Лист	Листов
РП	102	130

Развёртки стен В, Г. Кабинет (пом. 3)

М 1:40

Кырлан Александр Сергеевич

выпуск 19.10.2026 № 536a1f7ddae · стр. 108 из 160

Развёртки стен А, Б. Санузел гостевой (пом. 4)

Санузел гостевой (пом. 4) · вид изнутри помещения · размеры в мм, отметки в м

ПРЕДВАРИТЕЛЬНО · не для производства работ · открыто пунктов: 6 (реестр — л. 6)

Развёртка стены А

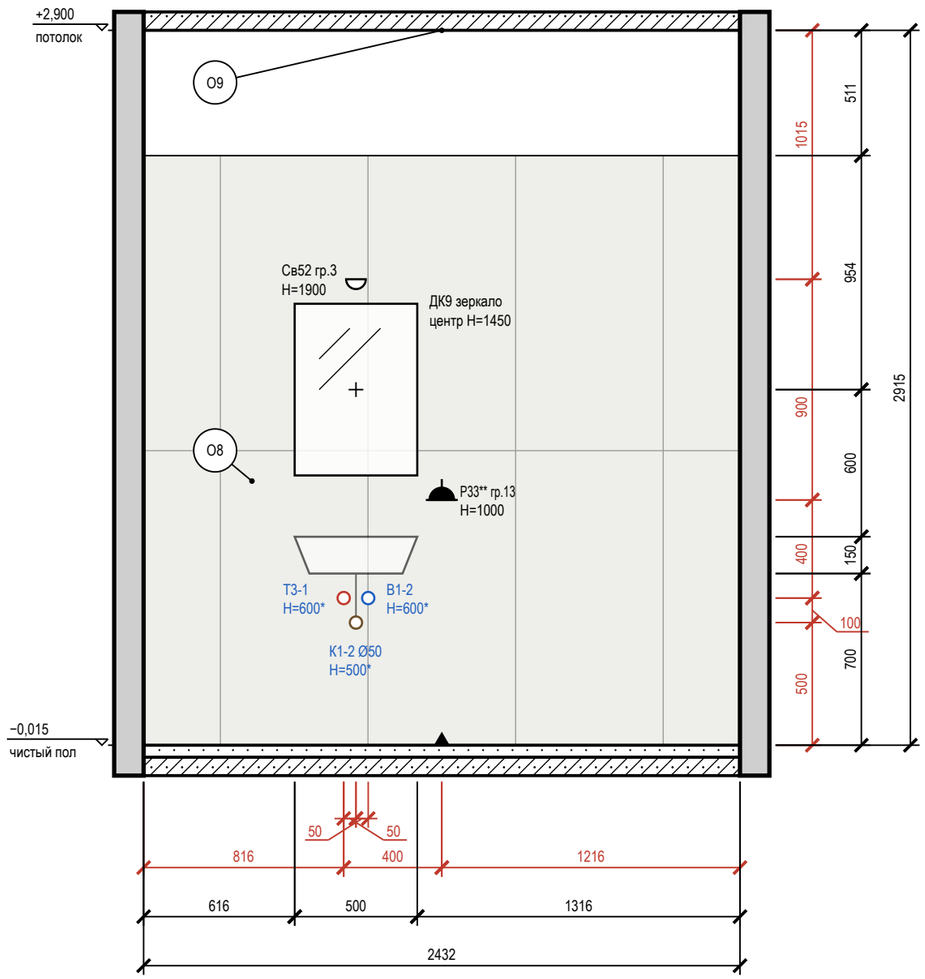

Развёртка стены Б

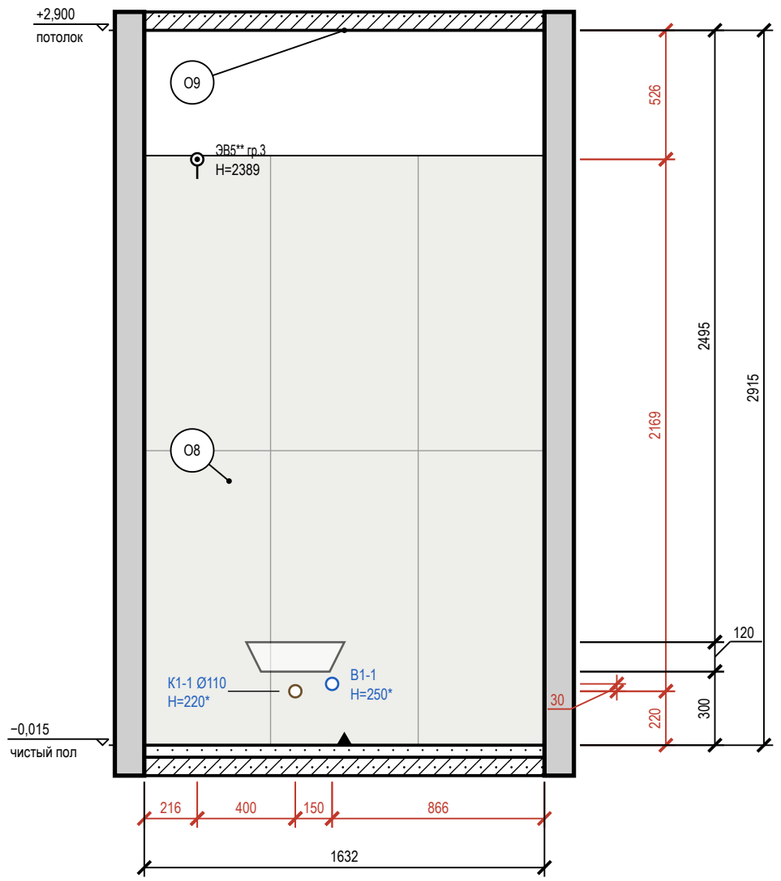

Схема развёрток (М 1:100)

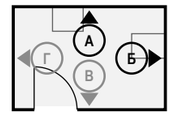

Условные обозначения

- розетка влагозащищённая IP44
- вывод кабеля для подключения прибора (без розетки), марка ЭВ
- светильник настенный (бра), H — высота оси
- вывод В1 (код — в ведомости привязок)
- вывод Т3 (код — в ведомости привязок)
- вывод К1 (код — в ведомости привязок)
- привязки точек и выводов от угла и от пола, мм
- мебель и приборы — фасад по расстановке (условно)
- зеркало: марка Д, крест — центр, H — высота центра, мм
- стены и перекрытия в сечении
- плитка: сетка швов по формату, ▲ — ось старта
- О1 — марка отделки по реестру отделки альбома
- А — марка развёртки: буква стены, стрелка — взгляд

Допущения и предложения на листе

Основа листа: взаимное расположение помещений, контур дома 9600 × 8000 и раскладка этажей подобраны проектировщиком под габариты помещений брифа; обмер и проект АР — задание (К-1); высота потолка 2900 мм — по брифу, не замерена; перекрытие 330 мм и отметка 2-го этажа +3,230 приняты; проект КР — задание (К-2); наружные стены 400 мм, перегородки 120 мм приняты (в брифе толщин нет) (К-1); разрешённая мощность 15 кВт принята по типовым ТУ для частного дома (К-4).

Знак «**» — предложение проектировщика, заказчиком не утверждено (согласовать с заказчиком): записи в реестре нет: Р33 — по образцу: Розетка Р33 на высоте 1100 мм, вне шва плитки; ЭВ5 — по образцу: Добавлены выводы к вентиляторам: ЭВ4 (ВР1, ванная) и ЭВ5 (ВР3, санузел 2) — группа 3, высота 2389 мм, включение с основным светом, таймер выбега в вентиляторе; и коробки уравнивания потенциалов КУП1 (ванная) и КУП2 (санузел 2) — высота 300 мм, у входа, вне зон 0–2, проводник от шины PE щита ЩК, сече.

См. лист открытых вопросов (лист 6, записи К-1, К-2, К-4).

Примечания

1. Развёртки — вид на стену изнутри помещения, по часовой стрелке; расположение — на схеме листа и на листе 94; размеры — в мм по чистовым поверхностям; отметки — в м от ±0,000; высоты H — от чистого пола помещения до оси изделия, у декора — до центра.
2. Красные цепочки — привязки электроточек и выводов: по горизонтали от угла чистовых стен, по вертикали от чистого пола, до оси изделия; звенья короче 3 мм на листе вынесены во второй ярус (ближняя к стене цепочка).
3. У знака электроточки: марка (Р — розетка, S — выключатель, Св — светильник, ЭВ — вывод кабеля), ×N — число постов в рамке, гр. — группа щита, H — высота оси от чистого пола, мм; группы по клавишам выключателя — на листе выключателей.
4. Схема мебели, приборов и декора не является технической документацией для производства мебели; габариты — по паспортам изделий (* — высота не задана в проекте, показана по типовому изделию).
5. Выводы ВК — коды и высоты по листу выводов сантехники; * — высота принята по типовой практике монтажа, окончательно — по паспорту прибора.
6. Облицовка — по сетке швов 2 мм, раскладка от оси стены (треугольник у пола), целые ряды от пола; подрезки — по листу раскладки плитки.
7. Гидроизоляция в 2 слоя, заход на стены 200 мм — до облицовки, с актом скрытых работ и тестом проливом (узел — на листе узлов).
8. Картины и зеркала крепить к основанию по паспорту изделия (закладные и анкеры — в перечне скрытых работ); крест — ось центра предмета.

1000 мм · печать 1:1

Изм.	Кол.уч	Лист	№ док.	Подп.	Дата
Разраб.		Кырлан А.С.			19.10.26
Пров.					
ГИП					
Н. контр.					
Утв.					

ГД-2026-012-АИ

Дом 120 м²

Общая площадь 147,36* м² · * размеры приняты, не замерены (реестр — л. 6, К-1)

Дизайн-проект интерьера	Стадия	Лист	Листов
	РП	103	130

Развёртки стен А, Б. Санузел гостевой (пом. 4)

М 1:25

Кырлан Александр Сергеевич

выпуск 19.10.2026 № 53e4f7ddae · стр. 109 из 160

Развёртки стен В, Г. Санузел гостевой (пом. 4)

Санузел гостевой (пом. 4) · вид изнутри помещения · размеры в мм, отметки в м

ПРЕДВАРИТЕЛЬНО · не для производства работ · открыто пунктов: 6 (реестр — л. 6)

Развёртка стены В

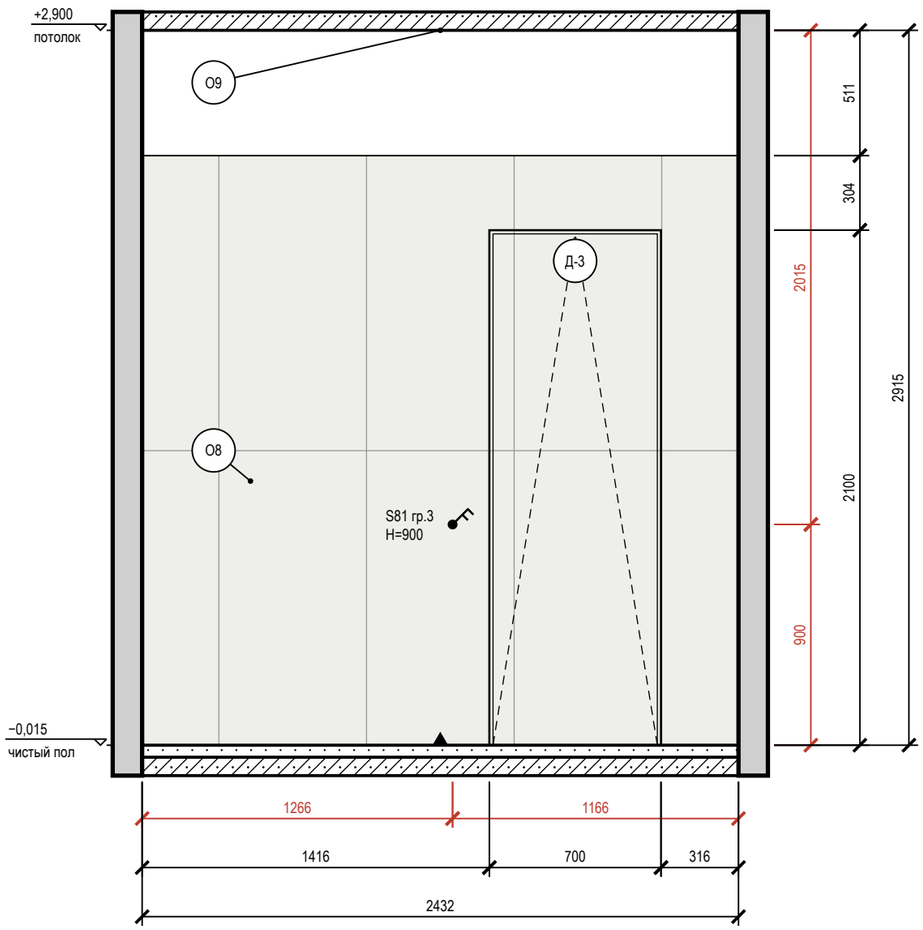

Развёртка стены Г

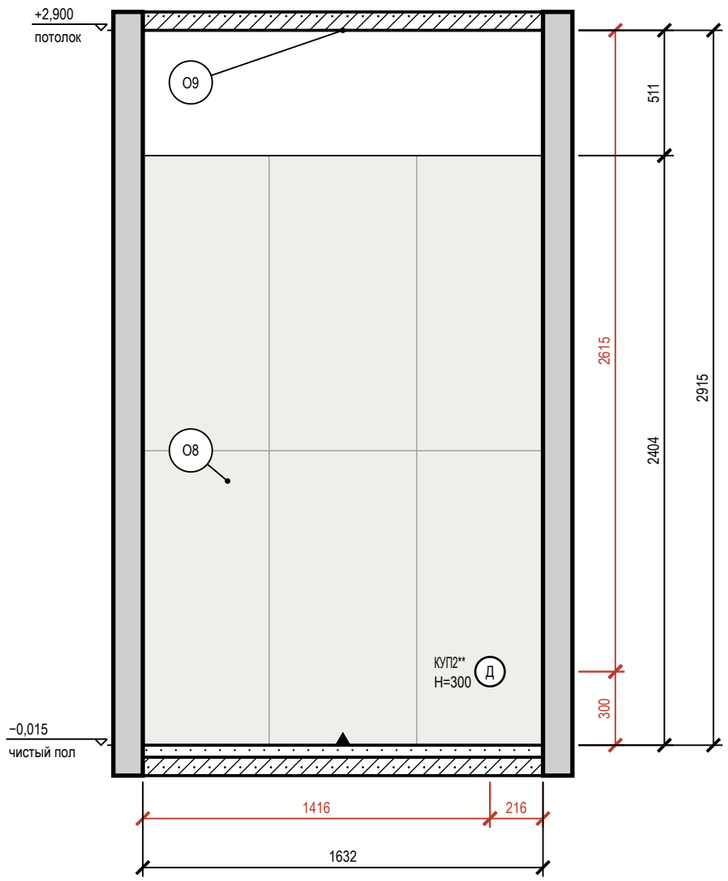

Условные обозначения

- выключатель одноклавишный
- выключатель двухклавишный (флажков — по числу клавиш)
- привязки точек и выводов от угла и от пола, мм
- мебель и приборы — фасад по расстановке (условно)
- дверь скрытого монтажа: полотно в плоскости стены (узел — на листе узлов)
- стены и перекрытия в сечении
- плитка: сетка швов по формату, ▲ — ось старта
- О1 — марка отделки по реестру отделки альбома
- А — марка развёртки: буква стены, стрелка — взгляд

Схема развёрток (М 1:100)

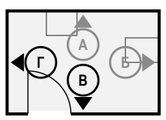

Ведомость отделки (на листе)

Марка	Поверхность	Материал, изделие	Цвет, код	Кол.
О8	стены	облицовка плиткой, Atlas Concorde Marvel Travertine, 600×1200×9 мм, A8UZ, затирка CG2WA	Atlas Concorde A8UZ «Marvel Travertine»	8,3 м²
О9	потолок	окраска, Tikkurila Luja 7, матовая, подготовка Q3	Little Greene No. 222 «Loft White»	4,2 м²

Допущения и предложения на листе

Основа листа: взаимное расположение помещений, контур дома 9600 × 8000 и раскладка этажей подобраны проектировщиком под габариты помещений брифа; обмер и проект АР — задание (К-1); высота потолка 2900 мм — по брифу, не замерена; перекрытие 330 мм и отметка 2-го этажа +3,230 приняты; проект КР — задание (К-2); наружные стены 400 мм, перегородки 120 мм приняты (в брифе толщин нет) (К-1); разрешённая мощность 15 кВт принята по типовым ТУ для частного дома (К-4).

Знак «**» — предложение проектировщика, заказчиком не утверждено (согласовать с заказчиком): записи в реестре нет: КУП2 — по образцу: Добавлены выводы к вентиляторам: ЭВ4 (ВР1, ванная) и ЭВ5 (ВР3, санузел 2) — группа 3, высота 2389 мм, включение с основным светом, таймер выбега в вентиляторе; и коробки уравнивания потенциалов КУП1 (ванная) и КУП2 (санузел 2) — высота 300 мм, у входа, вне зон 0–2, проводник от шины PE щита ЩК, сече.

См. лист открытых вопросов (лист 6, записи К-1, К-2, К-4).

Примечания

1. Развёртки — вид на стену изнутри помещения, по часовой стрелке; расположение — на схеме листа и на листе 94; размеры — в мм по чистовым поверхностям; отметки — в м от ±0,000; высоты H — от чистого пола помещения до оси изделия, у декора — до центра.
2. Красные цепочки — привязки электроточек и выводов: по горизонтали от угла чистовых стен, по вертикали от чистого пола, до оси изделия; звенья короче 3 мм на листе вынесены во второй ярус (ближняя к стене цепочка).
3. У знака электроточки: марка (Р — розетка, S — выключатель, Св — светильник, ЭВ — вывод кабеля), ×N — число постов в рамке, гр. — группа щита, H — высота оси от чистого пола, мм; группы по клавишам выключателя — на листе выключателей.
4. Схема мебели, приборов и декора не является технической документацией для производства мебели; габариты — по паспортам изделий.
5. Облицовка — по сетке швов 2 мм, раскладка от оси стены (треугольник у пола), целые ряды от пола; подрезки — по листу раскладки плитки.
6. Гидроизоляция в 2 слоя, заход на стены 200 мм — до облицовки, с актом скрытых работ и тестом проливом (узел — на листе узлов).
7. Двери скрытого монтажа — полотно в плоскости стены, отделка стены по полотну, плинтус прерывается у короба (узел — на листе узлов).

1000 мм · печать 1:1

Изм.	Кол.уч	Лист	№ док.	Подп.	Дата
Разраб.		Кырлан А.С.			19.10.26
Пров.					
ГИП					
Н. контр.					
Утв.					

ГД-2026-012-АИ

Дом 120 м²

Общая площадь 147,36* м² · * размеры приняты, не замерены (реестр — л. 6, К-1)

Дизайн-проект интерьера

Стадия	Лист	Листов
РП	104	130

Развёртки стен В, Г. Санузел гостевой (пом. 4)

М 1:25

Кырлан Александр Сергеевич

выпуск 19.10.2026 № 53e4f7ddae · стр. 110 из 160

Развёртки стен А1, А2, Б. Прихожая (пом. 5)

Прихожая (пом. 5) · вид изнутри помещения · размеры в мм, отметки в м

ПРЕДВАРИТЕЛЬНО · не для производства работ · открыто пунктов: 6 (реестр — л. 6)

Развёртка стены А1

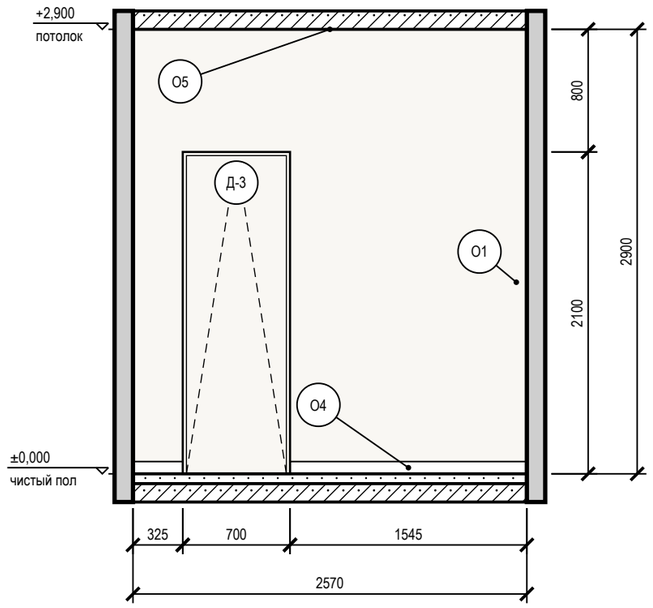

Развёртка стены А2

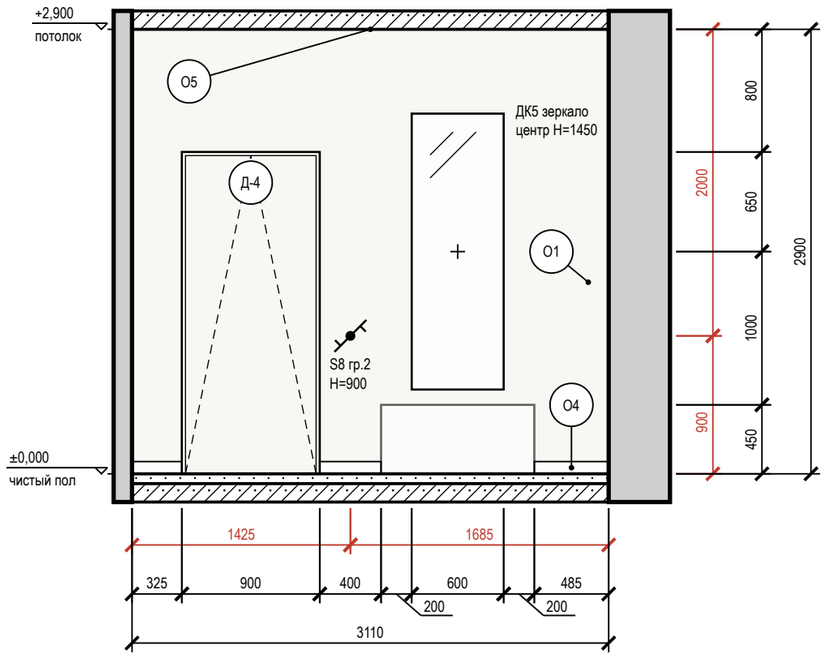

Развёртка стены Б

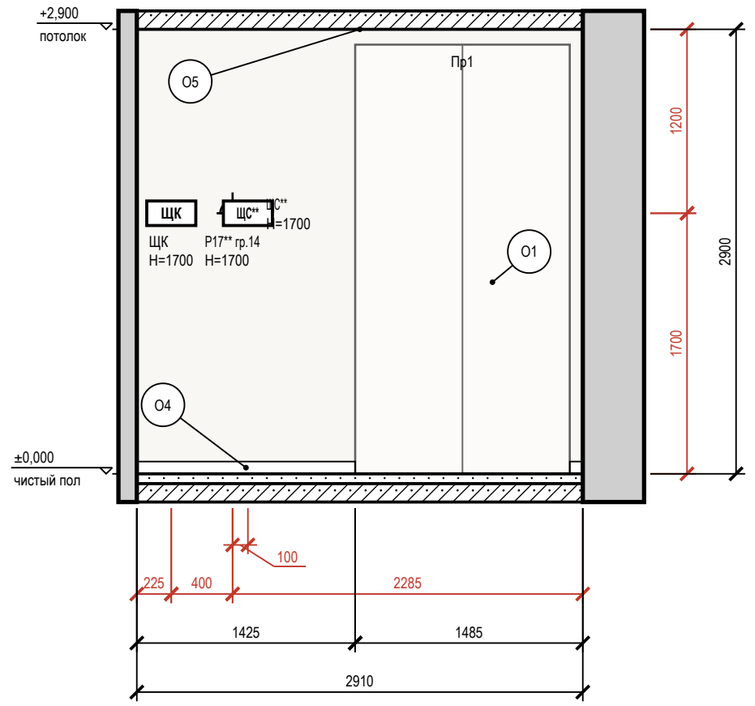

Схема развёрток (М 1:100)

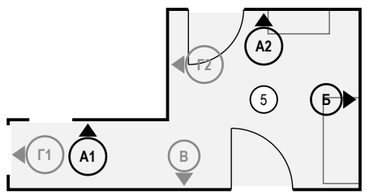

Условные обозначения

- розетка с заземляющим контактом; у знака — марка, ×N постов в рамке, гр. — группа щита, Н — высота оси, мм
- выключатель одноклавишный
- выключатель с проходной или перекрёстной клавишей (обратный флажок); тип клавиши — в подписи
- ЩК — щит квартирный
- привязки точек и выводов от угла и от пола, мм
- мебель и приборы — фасад по расстановке (условно)
- зеркало: марка Д, крест — центр, Н — высота центра, мм
- дверь скрытого монтажа: полотно в плоскости стены (узел — на листе узлов)
- стены и перекрытия в сечении
- окраска: тон — цвет по коду производителя (условно)
- О1 — марка отделки по реестру отделки альбома
- А — марка развёртки: буква стены, стрелка — взгляд

Ведомость отделки (на листе)

Марка	Поверхность	Материал, изделие	Цвет, код	Кол.
О1	стены	окраска, Farrow & Ball Modern Emulsion, матовая, подготовка Q3	Tikkurila G503 «Calla»	21,6 м²
О4	плинтус	плинтус МДФ, h 80 мм, аналог: плинтус МДФ под покраску 80×16	Tikkurila G503 «Calla»	4,6 м
О5	потолок	окраска, Tikkurila Anti-Reflex 2, глубокоматовая, подготовка Q3	Little Greene No. 222 «Loft White»	12,2 м²

Допущения и предложения на листе

Основа листа: взаимное расположение помещений, контур дома 9600 × 8000 и раскладка этажей подобраны проектировщиком под габариты помещений брифа; обмер и проект АР — задание (К-1); высота потолка 2900 мм — по брифу, не замерена; перекрытие 330 мм и отметка 2-го этажа +3,230 приняты; проект КР — задание (К-2); наружные стены 400 мм, перегородки 120 мм приняты (в брифе толщин нет) (К-1); разрешённая мощность 15 кВт принята по типовым ТУ для частного дома (К-4).

Знак «**» — предложение проектировщика, заказчиком не утверждено (согласовать с заказчиком): записи в реестре нет: Р17 — высота 1700 мм выше нормы 1 м (ПУЭ 6.6.30) по назначению: питание слаботочного щита ЩС, рядом со щитом на его высоте; ЩС — щит слаботочный: место и состав.

См. лист открытых вопросов (лист 6, записи К-1, К-2, К-4).

Примечания

1. Развёртки — вид на стену изнутри помещения, по часовой стрелке; расположение — на схеме листа и на листе 94; размеры — в мм по чистовым поверхностям; отметки — в м от ±0,000; высоты Н — от чистого пола помещения до оси изделия, у декора — до центра.
2. Красные цепочки — привязки электроточек и выводов: по горизонтали от угла чистовых стен, по вертикали от чистого пола, до оси изделия; звенья короче 3 мм на листе вынесены во второй ярус (ближняя к стене цепочка).
3. У знака электроточки: марка (Р — розетка, S — выключатель, Св — светильник, ЭВ — вывод кабеля), ×N — число постов в рамке, гр. — группа щита, Н — высота оси от чистого пола, мм; группы по клавишам выключателя — на листе выключателей.
4. Схема мебели, приборов и декора не является технической документацией для производства мебели; габариты — по паспортам изделий.
5. Картины и зеркала крепить к основанию по паспорту изделия (закладные и анкеры — в перечне скрытых работ); крест — ось центра предмета.
6. Двери скрытого монтажа — полотно в плоскости стены, отделка стены по полотну, плинтус прерывается у короба (узел — на листе узлов).

1000 мм · печать 1:1

Изм.	Кол.уч	Лист	№ док.	Подп.	Дата
Разраб.		Кырлан А.С.			19.10.26
Пров.					
ГИП					
Н. контр.					
Утв.					

ГД-2026-012-АИ

Дом 120 м²

Общая площадь 147,36* м² · * размеры приняты, не замерены (реестр — л. 6, К-1)

Дизайн-проект интерьера

Стадия	Лист	Листов
РП	105	130

Развёртки стен А1, А2, Б. Прихожая (пом. 5)

М 1:40

Кырлан Александр Сергеевич

выпуск 19.10.2026 № 53e4f7ddae · стр. 111 из 160

Развёртки стен В, Г1, Г2. Прихожая (пом. 5)

Прихожая (пом. 5) · вид изнутри помещения · размеры в мм, отметки в м

ПРЕДВАРИТЕЛЬНО · не для производства работ · открыто пунктов: 6 (реестр — л. 6)

Развёртка стены В

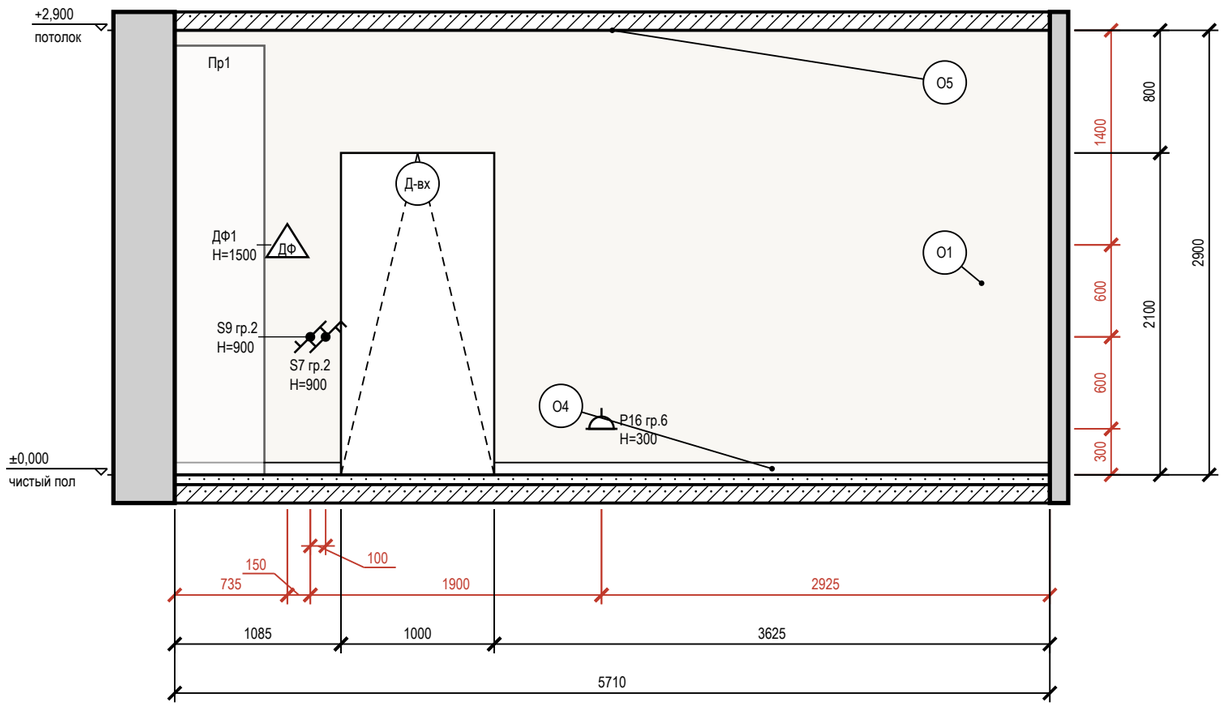

Развёртка стены Г1

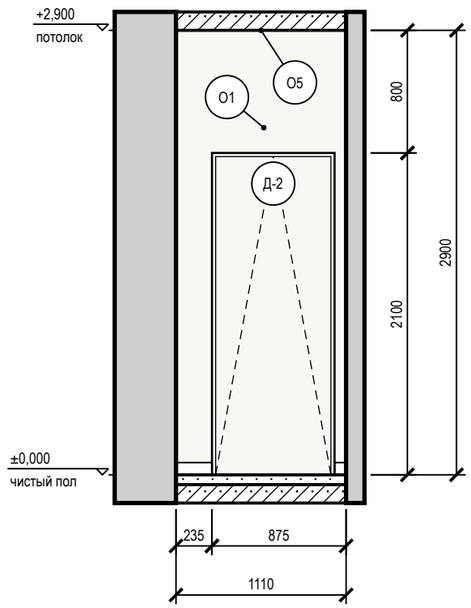

Развёртка стены Г2

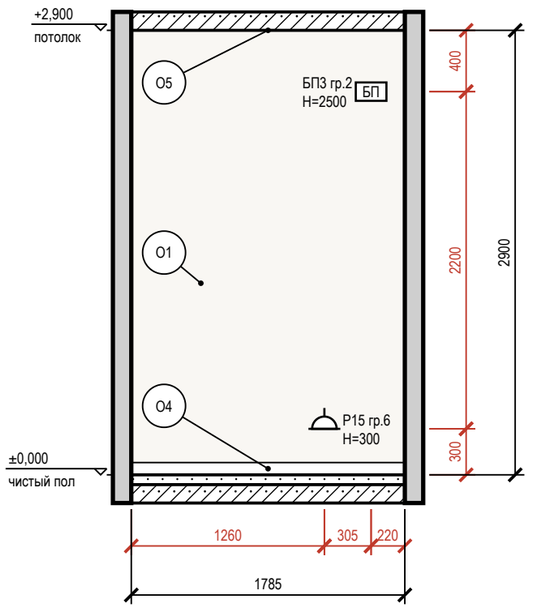

Схема развёрток (М 1:100)

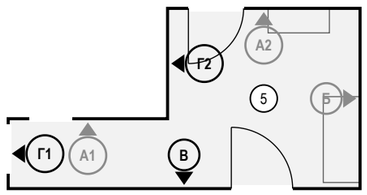

Условные обозначения

- розетка с заземляющим контактом; у знака — марка, ×N постов в рамке, гр. — группа щита, Н — высота оси, мм
- выключатель одноклавишный
- выключатель двухклавишный (флажков — по числу клавиш)
- выключатель с проходной или перекрёстной клавишей (обратный флажок); тип клавиши — в подписи
- БП — блок питания LED, с доступом (люк от 100×100 мм)
- ДФ — трубка или монитор домофона
- привязки точек и выводов от угла и от пола, мм
- мебель и приборы — фасад по расстановке (условно)
- дверь скрытого монтажа: полотно в плоскости стены (узел — на листе узлов)
- дверной проём; марка двери — в кружке
- стены и перекрытия в сечении
- окраска: тон — цвет по коду производителя (условно)
- О1 — марка отделки по реестру отделки альбома
- А — марка развёртки: буква стены, стрелка — взгляд

Ведомость отделки (на листе)

Марка	Поверхность	Материал, изделие	Цвет, код	Кол.
О1	стены	окраска, Farrow & Ball Modern Emulsion, матовая, подготовка Q3	Tikkurila G503 «Calla»	21,2 м²
О4	плинтус	плинтус МДФ, h 80 мм, аналог: плинтус МДФ под покраску 80×16	Tikkurila G503 «Calla»	6,8 м
О5	потолок	окраска, Tikkurila Anti-Reflex 2, глубокоматовая, подготовка Q3	Little Greene No. 222 «Loft White»	12,2 м²

Допущения и предложения на листе

Основа листа: взаимное расположение помещений, контур дома 9600 × 8000 и раскладка этажей подобраны проектировщиком под габариты помещений брифа; обмер и проект АР — задание (К-1); высота потолка 2900 мм — по брифу, не замерена; перекрытие 330 мм и отметка 2-го этажа +3,230 приняты; проект КР — задание (К-2); наружные стены 400 мм, перегородки 120 мм приняты (в брифе толщин нет) (К-1); разрешённая мощность 15 кВт принята по типовым ТУ для частного дома (К-4).
См. лист открытых вопросов (лист 6, записи К-1, К-2, К-4).

Примечания

1. Развёртки — вид на стену изнутри помещения, по часовой стрелке; расположение — на схеме листа и на листе 94; размеры — в мм по чистовым поверхностям; отметки — в м от ±0,000; высоты Н — от чистого пола помещения до оси изделия, у декора — до центра.
2. Красные цепочки — привязки электроточек и выводов: по горизонтали от угла чистовых стен, по вертикали от чистого пола, до оси изделия; звенья короче 3 мм на листе вынесены во второй ярус (ближняя к стене цепочка).
3. У знака электроточки: марка (Р — розетка, S — выключатель, Св — светильник, ЭВ — вывод кабеля), ×N — число постов в рамке, гр. — группа щита, Н — высота оси от чистого пола, мм; группы по клавишам выключателя — на листе выключателей.
4. Схема мебели, приборов и декора не является технической документацией для производства мебели; габариты — по паспортам изделий.
5. Двери скрытого монтажа — полотно в плоскости стены, отделка стены по полотну, плинтус прерывается у короба (узел — на листе узлов).

1000 мм · печать 1:1

Изм.	Кол.уч	Лист	№ док.	Подп.	Дата
Разраб.		Кырлан А.С.			19.10.26
Пров.					
ГИП					
Н. контр.					
Утв.					

ГД-2026-012-АИ

Дом 120 м²

Общая площадь 147,36* м² · * размеры приняты, не замерены (реестр — л. 6, К-1)

Дизайн-проект интерьера

Стадия	Лист	Листов
РП	106	130

Развёртки стен В, Г1, Г2. Прихожая (пом. 5)

М 1:40

Кырлан Александр Сергеевич

выпуск 19.10.2026 № 53e4f7ddae · стр. 112 из 160

Развёртки стен А, Б. Спальня родителей (пом. 6)

Спальня родителей (пом. 6) · вид изнутри помещения · размеры в мм, отметки в м

ПРЕДВАРИТЕЛЬНО · не для производства работ · открыто пунктов: 6 (реестр — л. 6)

Развёртка стены А

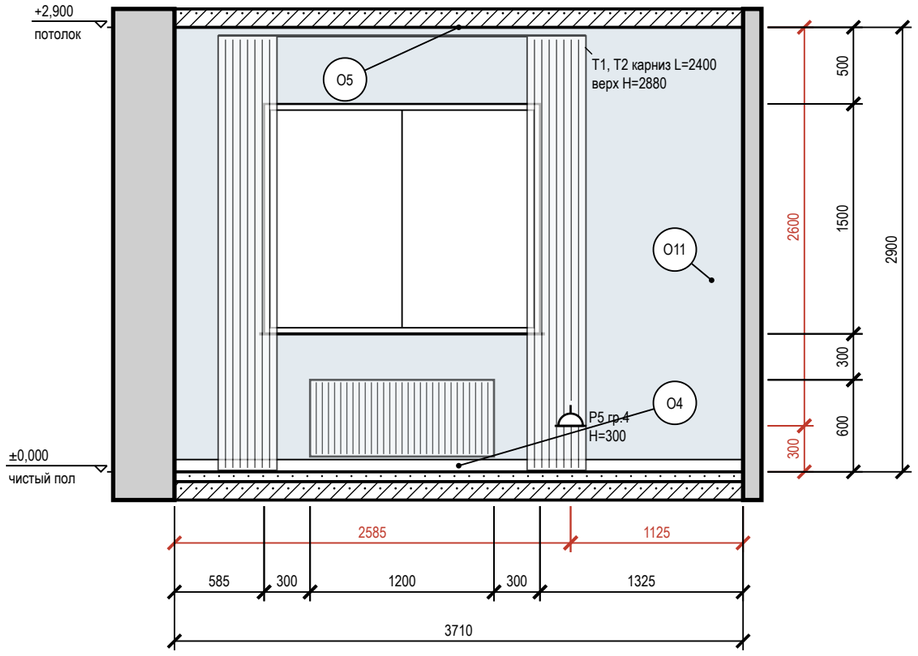

Развёртка стены Б

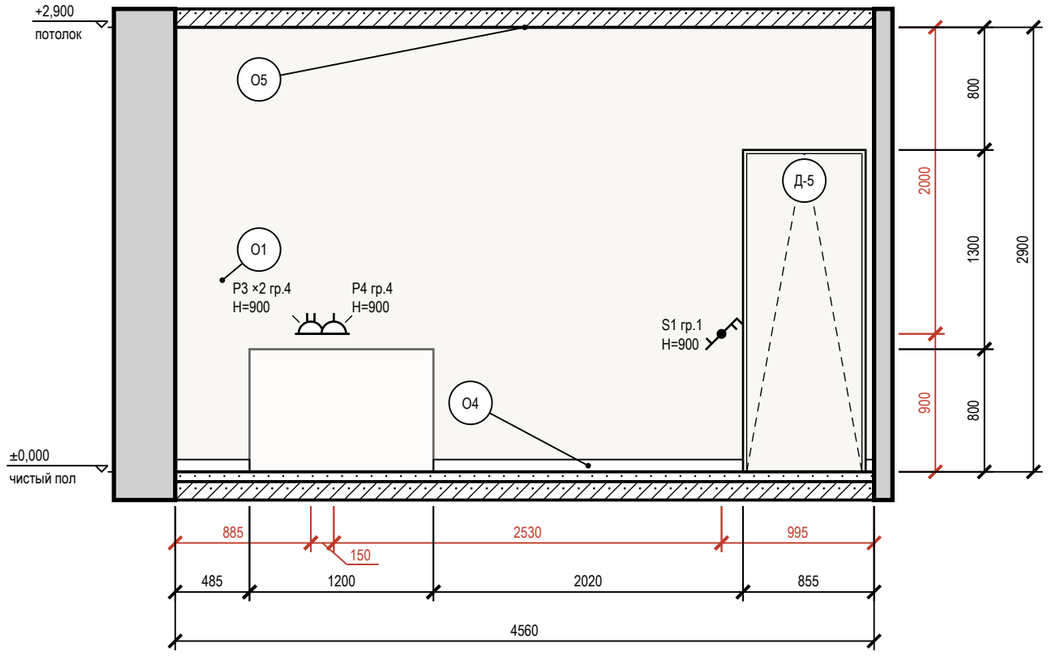

Схема развёрток (М 1:100)

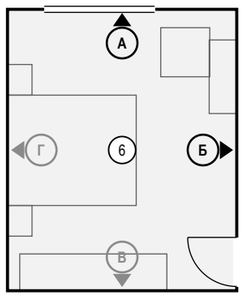

Условные обозначения

- розетка с заземляющим контактом; у знака — марка, ×N постов в рамке, гр. — группа щита, H — высота оси, мм
- выключатель одноклавишный
- выключатель двухклавишный (флажков — по числу клавиш)
- выключатель с проходной или перекрёстной клавишей (обратный флажок); тип клавиши — в подписи
- привязки точек и выводов от угла и от пола, мм
- мебель и приборы — фасад по расстановке (условно)
- карниз (шина) и шторы в собранном виде: марка Т, длина L, верх H
- дверь скрытого монтажа: полотно в плоскости стены (узел — на листе узлов)
- окно: проём, рама, подоконник
- радиатор отопления; марка — по плану отопления
- стены и перекрытия в сечении
- окраска: тон — цвет по коду производителя (условно)
- О1 — марка отделки по реестру отделки альбома
- А — марка развёртки: буква стены, стрелка — взгляд

Ведомость отделки (на листе)

Марка	Поверхность	Материал, изделие	Цвет, код	Кол.
О1	стены	окраска, Farrow & Ball Modern Emulsion, матовая, подготовка Q3	Tikkurila G503 «Calla»	11,5 м²
О4	плинтус	плинтус МДФ, h 80 мм, аналог: плинтус МДФ под покраску 80×16	Tikkurila G503 «Calla»	6,3 м
О5	потолок	окраска, Tikkurila Anti-Reflex 2, глубокоматовая, подготовка Q3	Little Greene No. 222 «Loft White»	17,2 м²
О11	акцентная стена	окраска, Farrow & Ball Modern Emulsion, матовая, подготовка Q3	Farrow & Ball No. 89 «Lulworth Blue — светлая морская лазурь»	8,1 м²

Допущения и предложения на листе

Основа листа: взаимное расположение помещений, контур дома 9600 × 8000 и раскладка этажей подобраны проектировщиком под габариты помещений брифа; обмер и проект АР — задание (К-1); высота потолка 2900 мм — по брифу, не замерена; перекрытие 330 мм и отметка 2-го этажа +3,230 приняты; проект КР — задание (К-2); наружные стены 400 мм, перегородки 120 мм приняты (в брифе толщин нет) (К-1); разрешённая мощность 15 кВт принята по типовым ТУ для частного дома (К-4).
См. лист открытых вопросов (лист 6, записи К-1, К-2, К-4).

Примечания

1. Развёртки — вид на стену изнутри помещения, по часовой стрелке; расположение — на схеме листа и на листе 94; размеры — в мм по чистовым поверхностям; отметки — в м от ±0,000; высоты H — от чистого пола помещения до оси изделия, у декора — до центра.
2. Красные цепочки — привязки электроточек и выводов: по горизонтали от угла чистовых стен, по вертикали от чистого пола, до оси изделия; звенья короче 3 мм на листе вынесены во второй ярус (ближняя к стене цепочка).
3. У знака электроточки: марка (Р — розетка, S — выключатель, Св — светильник, ЭВ — вывод кабеля), ×N — число постов в рамке, гр. — группа щита, H — высота оси от чистого пола, мм; группы по клавишам выключателя — на листе выключателей.
4. Схема мебели, приборов и декора не является технической документацией для производства мебели; габариты — по паспортам изделий.
5. Карнизы (шины) — по ведомости текстиля декоратора; длина L и верх H — по развёртке, крепление — до окраски потолка.
6. Двери скрытого монтажа — полотно в плоскости стены, отделка стены по полотну, плинтус прерывается у короба (узел — на листе узлов).
7. Линии узора (швы плитки, складки штор, рёбра радиаторов) прерываются у знаков и выносок — просвет между линиями не менее 0,7 мм.

1000 мм · печать 1:1

Изм.	Кол.уч	Лист	№ док.	Подп.	Дата
Разраб.		Кырлан А.С.			19.10.26
Пров.					
ГИП					
Н. контр.					
Утв.					

ГД-2026-012-АИ

Дом 120 м²

Общая площадь 147,36* м² · * размеры приняты, не замерены (реестр — л. 6, К-1)

Дизайн-проект интерьера

Стадия	Лист	Листов
РП	107	130

Развёртки стен А, Б. Спальня родителей (пом. 6)

М 1:40

Кырлан Александр Сергеевич

выпуск 19.10.2026 № 53e4f7ddae · стр. 113 из 160

Развёртки стен В, Г. Спальня родителей (пом. 6)

Спальня родителей (пом. 6) · вид изнутри помещения · размеры в мм, отметки в м

ПРЕДВАРИТЕЛЬНО · не для производства работ · открыто пунктов: 6 (реестр — л. 6)

Развёртка стены В

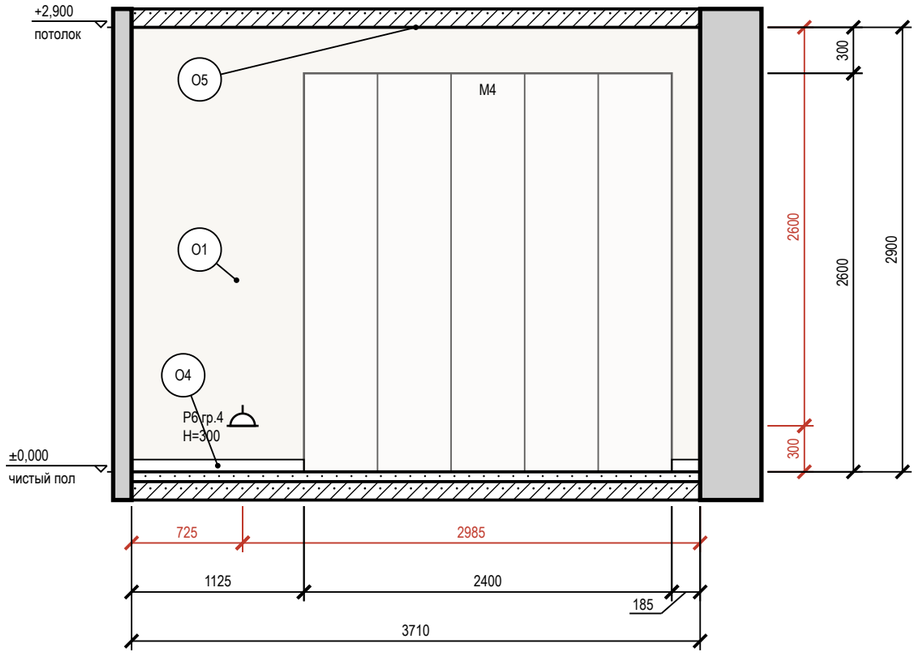

Развёртка стены Г

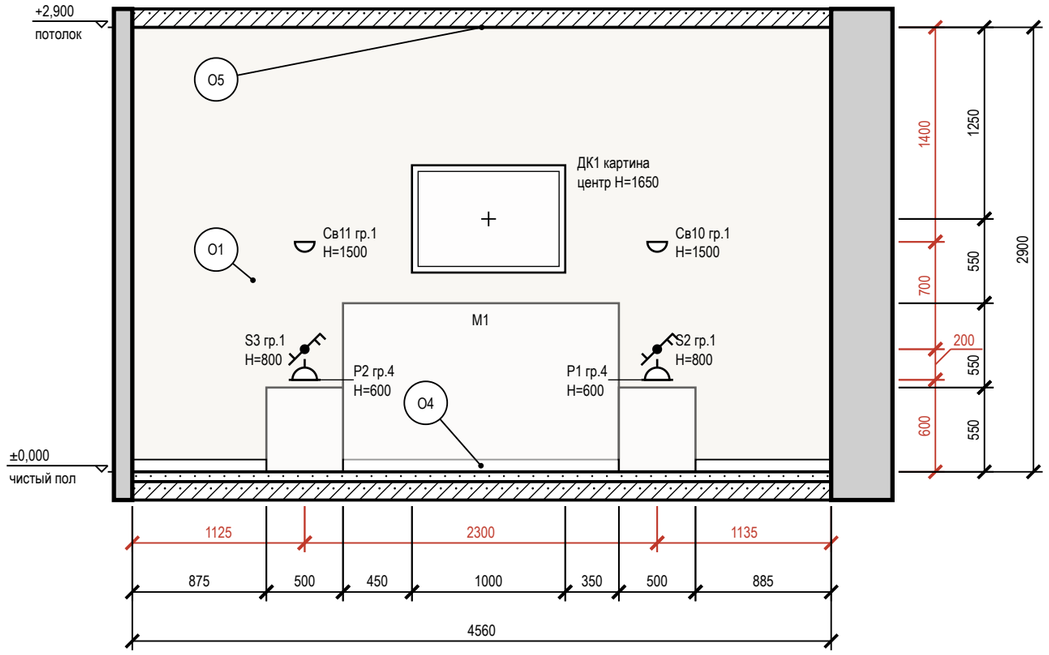

Схема развёрток (М 1:100)

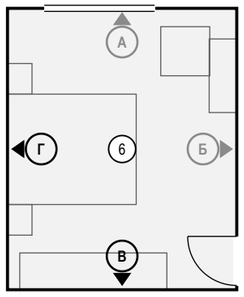

Условные обозначения

- розетка с заземляющим контактом; у знака — марка, ×N постов в рамке, гр. — группа щита, Н — высота оси, мм
- выключатель одноклавишный
- выключатель двухклавишный (флажков — по числу клавиш)
- выключатель с проходной или перекрёстной клавишей (обратный флажок); тип клавиши — в подписи
- светильник настенный (бра), Н — высота оси
- привязки точек и выводов от угла и от пола, мм
- мебель и приборы — фасад по расстановке (условно)
- картина (декор): марка Д, крест — центр, Н — высота центра, мм
- стены и перекрытия в сечении
- окраска: тон — цвет по коду производителя (условно)
- О1 — марка отделки по реестру отделки альбома
- А — марка развёртки: буква стены, стрелка — взгляд

Ведомость отделки (на листе)

Марка	Поверхность	Материал, изделие	Цвет, код	Кол.
О1	стены	окраска, Farrow & Ball Modern Emulsion, матовая, подготовка Q3	Tikkurila G503 «Calla»	24 м²
О4	плинтус	плинтус МДФ, h 80 мм, аналог: плинтус МДФ под покраску 80×16	Tikkurila G503 «Calla»	4,9 м
О5	потолок	окраска, Tikkurila Anti-Reflex 2, глубокоматовая, подготовка Q3	Little Greene No. 222 «Loft White»	17,2 м²

Допущения и предложения на листе

Основа листа: взаимное расположение помещений, контур дома 9600 × 8000 и раскладка этажей подобраны проектировщиком под габариты помещений брифа; обмер и проект АР — задание (К-1); высота потолка 2900 мм — по брифу, не замерена; перекрытие 330 мм и отметка 2-го этажа +3,230 приняты; проект КР — задание (К-2); наружные стены 400 мм, перегородки 120 мм приняты (в брифе толщин нет) (К-1); разрешённая мощность 15 кВт принята по типовым ТУ для частного дома (К-4).
См. лист открытых вопросов (лист 6, записи К-1, К-2, К-4).

Примечания

1. Развёртки — вид на стену изнутри помещения, по часовой стрелке; расположение — на схеме листа и на листе 94; размеры — в мм по чистовым поверхностям; отметки — в м от ±0,000; высоты Н — от чистого пола помещения до оси изделия, у декора — до центра.
2. Красные цепочки — привязки электроточек и выводов: по горизонтали от угла чистовых стен, по вертикали от чистого пола, до оси изделия; звенья короче 3 мм на листе вынесены во второй ярус (ближняя к стене цепочка).
3. У знака электроточки: марка (Р — розетка, S — выключатель, Св — светильник, ЭВ — вывод кабеля), ×N — число постов в рамке, гр. — группа щита, Н — высота оси от чистого пола, мм; группы по клавишам выключателя — на листе выключателей.
4. Схема мебели, приборов и декора не является технической документацией для производства мебели; габариты — по паспортам изделий.
5. Картины и зеркала крепить к основанию по паспорту изделия (закладные и анкеры — в перечне скрытых работ); крест — ось центра предмета.

1000 мм · печать 1:1

Изм.	Кол.уч	Лист	№ док.	Подп.	Дата
Разраб.		Кырлан А.С.			19.10.26
Пров.					
ГИП					
Н. контр.					
Утв.					

ГД-2026-012-АИ

Дом 120 м²

Общая площадь 147,36* м² · * размеры приняты, не замерены (реестр — л. 6, К-1)

Дизайн-проект интерьера	Стадия	Лист	Листов
	РП	108	130

Развёртки стен В, Г. Спальня родителей (пом. 6)

М 1:40

Кырлан Александр Сергеевич

выпуск 19.10.2026 № 536477ddae · стр. 114 из 160

Развёртки стен А, Б. Детская (пом. 7)

Детская (пом. 7) · вид изнутри помещения · размеры в мм, отметки в м

ПРЕДВАРИТЕЛЬНО · не для производства работ · открыто пунктов: 6 (реестр — л. 6)

Развёртка стены А

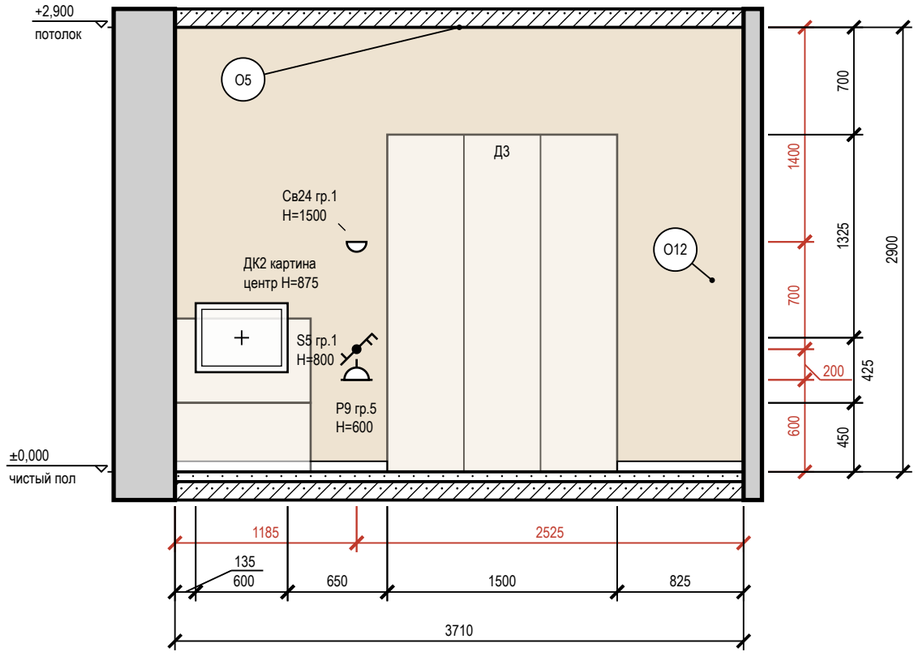

Развёртка стены Б

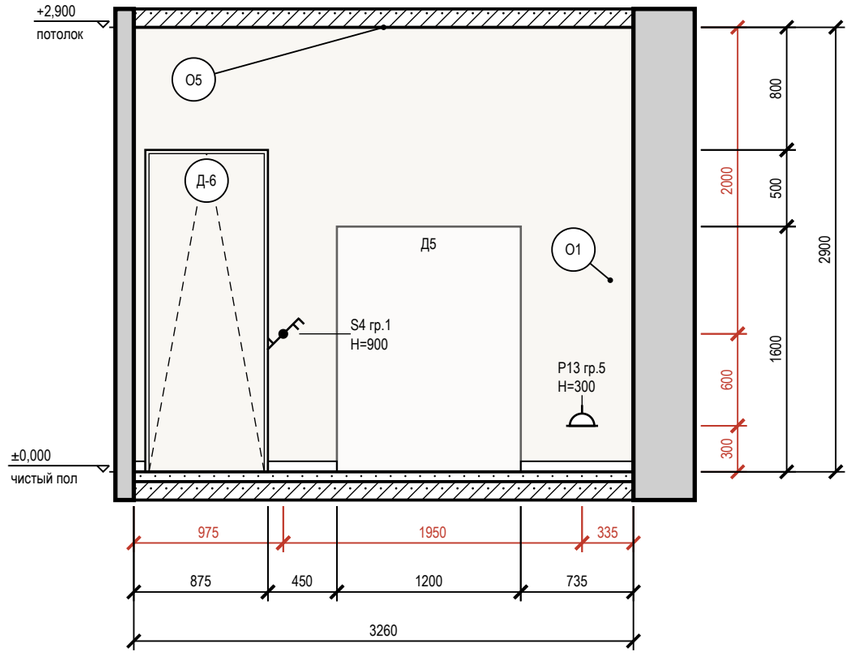

Схема развёрток (М 1:100)

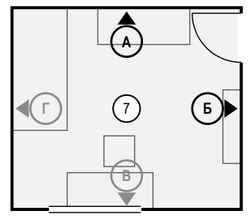

Условные обозначения

- розетка с заземляющим контактом; у знака — марка, ×N постов в рамке, гр. — группа щита, Н — высота оси, мм
- выключатель одноклавишный
- выключатель двухклавишный (флажков — по числу клавиш)
- выключатель с проходной или перекрёстной клавишей (обратный флажок); тип клавиши — в подписи
- светильник настенный (бра), Н — высота оси
- привязки точек и выводов от угла и от пола, мм
- мебель и приборы — фасад по расстановке (условно)
- картина (декор): марка Д, крест — центр, Н — высота центра, мм
- дверь скрытого монтажа: полотно в плоскости стены (узел — на листе узлов)
- стены и перекрытия в сечении
- окраска: тон — цвет по коду производителя (условно)
- О1 — марка отделки по реестру отделки альбома
- А — марка развёртки: буква стены, стрелка — взгляд

Ведомость отделки (на листе)

Марка	Поверхность	Материал, изделие	Цвет, код	Кол.
О1	стены	окраска, Farrow & Ball Modern Emulsion, матовая, подготовка Q3	Tikkurila G503 «Calla»	7,8 м²
О5	потолок	окраска, Tikkurila Anti-Reflex 2, глубокоматовая, подготовка Q3	Little Greene No. 222 «Loft White»	12,3 м²
О12	акцентная стена	окраска, Farrow & Ball Modern Emulsion, матовая, подготовка Q3	Farrow & Ball No. 66 «India Yellow — охра / горчица итальянских фасадов»	10,8 м²
О13	плинтус	плинтус МДФ, Orac Decor Contour (Luxxus), h 69 мм, SX165	Tikkurila G503 «Calla»	3,5 м

Допущения и предложения на листе

Основа листа: взаимное расположение помещений, контур дома 9600 × 8000 и раскладка этажей подобраны проектировщиком под габариты помещений брифа; обмер и проект АР — задание (К-1); высота потолка 2900 мм — по брифу, не замерена; перекрытие 330 мм и отметка 2-го этажа +3,230 приняты; проект КР — задание (К-2); наружные стены 400 мм, перегородки 120 мм приняты (в брифе толщин нет) (К-1); разрешённая мощность 15 кВт принята по типовым ТУ для частного дома (К-4).
См. лист открытых вопросов (лист 6, записи К-1, К-2, К-4).

Примечания

1. Развёртки — вид на стену изнутри помещения, по часовой стрелке; расположение — на схеме листа и на листе 94; размеры — в мм по чистовым поверхностям; отметки — в м от ±0,000; высоты Н — от чистого пола помещения до оси изделия, у декора — до центра.
2. Красные цепочки — привязки электроточек и выводов: по горизонтали от угла чистовых стен, по вертикали от чистого пола, до оси изделия; звенья короче 3 мм на листе вынесены во второй ярус (ближняя к стене цепочка).
3. У знака электроточки: марка (Р — розетка, S — выключатель, Св — светильник, ЭВ — вывод кабеля), ×N — число постов в рамке, гр. — группа щита, Н — высота оси от чистого пола, мм; группы по клавишам выключателя — на листе выключателей.
4. Схема мебели, приборов и декора не является технической документацией для производства мебели; габариты — по паспортам изделий.
5. Картины и зеркала крепить к основанию по паспорту изделия (закладные и анкеры — в перечне скрытых работ); крест — ось центра предмета.
6. Двери скрытого монтажа — полотно в плоскости стены, отделка стены по полотну, плинтус прерывается у короба (узел — на листе узлов).

1000 мм · печать 1:1

Изм.	Кол.уч	Лист	№ док.	Подп.	Дата
Разраб.		Кырлан А.С.			19.10.26
Пров.					
ГИП					
Н. контр.					
Утв.					

ГД-2026-012-АИ

Дом 120 м²

Общая площадь 147,36* м² · * размеры приняты, не замерены (реестр — л. 6, К-1)

Дизайн-проект интерьера

Стадия	Лист	Листов
РП	109	130

Развёртки стен А, Б. Детская (пом. 7)

М 1:40

Кырлан Александр Сергеевич

выпуск 19.10.2026 № 53e4f7ddae · стр. 115 из 160

Развёртки стен В, Г. Детская (пом. 7)

Детская (пом. 7) · вид изнутри помещения · размеры в мм, отметки в м

ПРЕДВАРИТЕЛЬНО · не для производства работ · открыто пунктов: 6 (реестр — л. 6)

Развёртка стены В

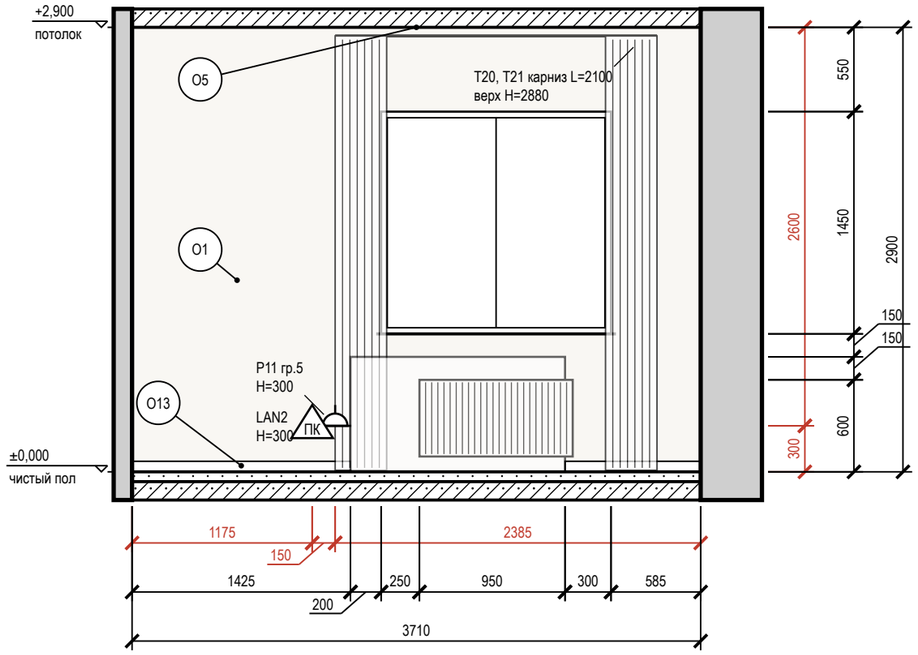

Развёртка стены Г

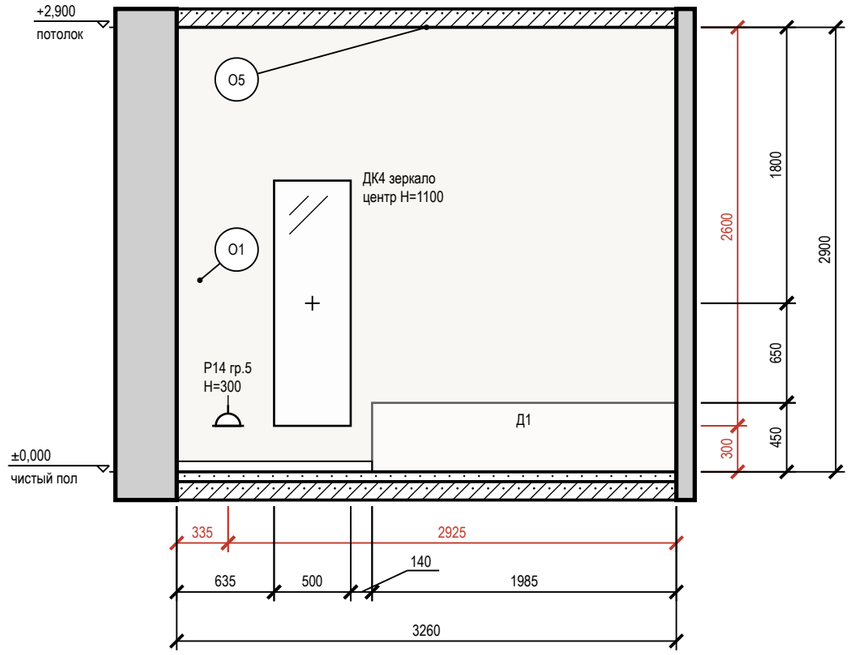

Схема развёрток (М 1:100)

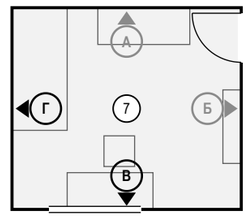

Условные обозначения

- розетка с заземляющим контактом; у знака — марка, ×N постов в рамке, гр. — группа щита, Н — высота оси, мм
- ПК — розетка компьютерная RJ45
- привязки точек и выводов от угла и от пола, мм
- мебель и приборы — фасад по расстановке (условно)
- зеркало: марка Д, крест — центр, Н — высота центра, мм
- карниз (шина) и шторы в собранном виде: марка Т, длина L, верх Н
- окно: проём, рама, подоконник
- радиатор отопления; марка — по плану отопления
- стены и перекрытия в сечении
- окраска: тон — цвет по коду производителя (условно)
- О1 — марка отделки по реестру отделки альбома
- А — марка развёртки: буква стены, стрелка — взгляд

Ведомость отделки (на листе)

Марка	Поверхность	Материал, изделие	Цвет, код	Кол.
О1	стены	окраска, Farrow & Ball Modern Emulsion, матовая, подготовка Q3	Tikkurila G503 «Calla»	18 м²
О5	потолок	окраска, Tikkurila Anti-Reflex 2, глубокоматовая, подготовка Q3	Little Greene No. 222 «Loft White»	12,3 м²
О13	плинтус	плинтус МДФ, Orac Decor Contour (Luxxus), h 69 мм, SX165	Tikkurila G503 «Calla»	3,6 м

Допущения и предложения на листе

Основа листа: взаимное расположение помещений, контур дома 9600 × 8000 и раскладка этажей подобраны проектировщиком под габариты помещений брифа; обмер и проект АР — задание (К-1); высота потолка 2900 мм — по брифу, не замерена; перекрытие 330 мм и отметка 2-го этажа +3,230 приняты; проект КР — задание (К-2); наружные стены 400 мм, перегородки 120 мм приняты (в брифе толщин нет) (К-1); разрешённая мощность 15 кВт принята по типовым ТУ для частного дома (К-4).
См. лист открытых вопросов (лист 6, записи К-1, К-2, К-4).

Примечания

1. Развёртки — вид на стену изнутри помещения, по часовой стрелке; расположение — на схеме листа и на листе 94; размеры — в мм по чистовым поверхностям; отметки — в м от ±0,000; высоты Н — от чистого пола помещения до оси изделия, у декора — до центра.
2. Красные цепочки — привязки электроточек и выводов: по горизонтали от угла чистовых стен, по вертикали от чистого пола, до оси изделия; звенья короче 3 мм на листе вынесены во второй ярус (ближняя к стене цепочка).
3. У знака электроточки: марка (Р — розетка, S — выключатель, Св — светильник, ЭВ — вывод кабеля), ×N — число постов в рамке, гр. — группа щита, Н — высота оси от чистого пола, мм; группы по клавишам выключателя — на листе выключателей.
4. Схема мебели, приборов и декора не является технической документацией для производства мебели; габариты — по паспортам изделий.
5. Картины и зеркала крепить к основанию по паспорту изделия (закладные и анкеры — в перечне скрытых работ); крест — ось центра предмета.
6. Карнизы (шины) — по ведомости текстиля декоратора; длина L и верх Н — по развёртке, крепление — до окраски потолка.

1000 мм · печать 1:1

Изм.	Кол.уч	Лист	№ док.	Подп.	Дата
Разраб.		Кырлан А.С.			19.10.26
Пров.					
ГИП					
Н. контр.					
Утв.					

ГД-2026-012-АИ

Дом 120 м²

Общая площадь 147,36* м² · * размеры приняты, не замерены (реестр — л. 6, К-1)

Дизайн-проект интерьера

Стадия	Лист	Листов
РП	110	130

Развёртки стен В, Г. Детская (пом. 7)

М 1:40

Кырлан Александр Сергеевич

выпуск 19.10.2026 № 536477ddae · стр. 116 из 160

Развёртки стен А, Б, В. Гардеробная (пом. 8)

Гардеробная (пом. 8) · вид изнутри помещения · размеры в мм, отметки в м

ПРЕДВАРИТЕЛЬНО · не для производства работ · открыто пунктов: 6 (реестр — л. 6)

Развёртка стены А

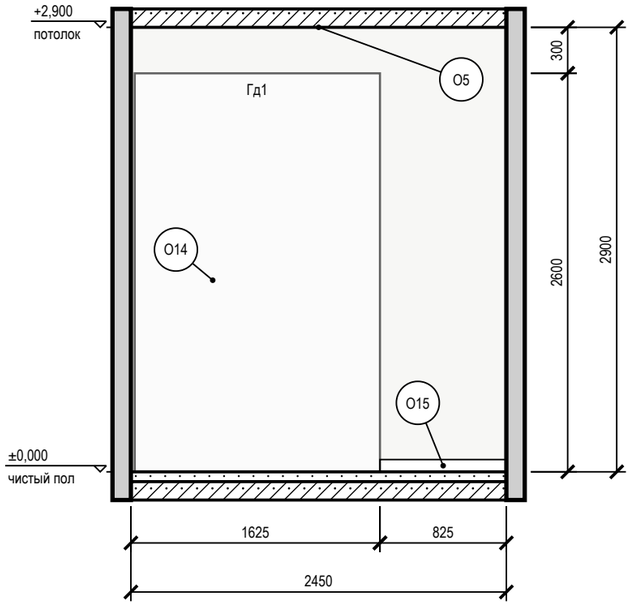

Развёртка стены Б

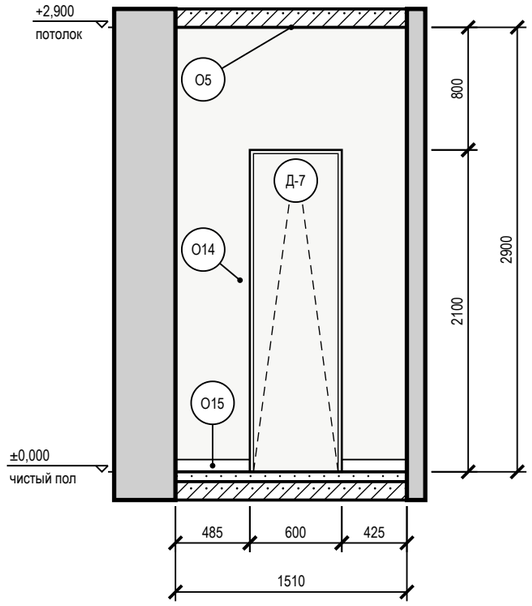

Развёртка стены В

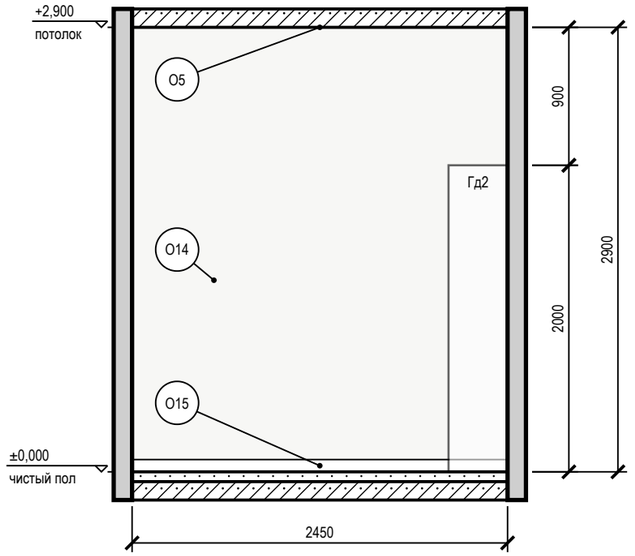

Схема развёрток (М 1:100)

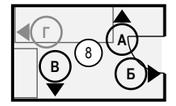

Условные обозначения

- привязки точек и выводов от угла и от пола, мм
- мебель и приборы — фасад по расстановке (условно)
- дверь скрытого монтажа: полотно в плоскости стены (узел — на листе узлов)
- стены и перекрытия в сечении
- окраска: тон — цвет по коду производителя (условно)
- О1 — марка отделки по реестру отделки альбома
- А — марка развёртки: буква стены, стрелка — взгляд

Ведомость отделки (на листе)

Марка	Поверхность	Материал, изделие	Цвет, код	Кол.
О5	потолок	окраска, Tikkurila Anti-Reflex 2, глубокоматовая, подготовка Q3	Little Greene No. 222 «Loft White»	3,8 м²
О14	стены	окраска, Tikkurila Harmony, матовая, подготовка Q3	Little Greene No. 222 «Loft White»	17,3 м²
О15	плинтус	плинтус МДФ, h 80 мм, аналог: плинтус МДФ под покраску 80×16	Little Greene No. 222 «Loft White»	4,2 м

Допущения и предложения на листе

Основа листа: взаимное расположение помещений, контур дома 9600 × 8000 и раскладка этажей подобраны проектировщиком под габариты помещений брифа; обмер и проект АР — задание (К-1); высота потолка 2900 мм — по брифу, не замерена; перекрытие 330 мм и отметка 2-го этажа +3,230 приняты; проект КР — задание (К-2); наружные стены 400 мм, перегородки 120 мм приняты (в брифе толщин нет) (К-1); разрешённая мощность 15 кВт принята по типовым ТУ для частного дома (К-4).
См. лист открытых вопросов (лист 6, записи К-1, К-2, К-4).

Примечания

1. Развёртки — вид на стену изнутри помещения, по часовой стрелке; расположение — на схеме листа и на листе 94; размеры — в мм по чистовым поверхностям; отметки — в м от ±0,000; высоты Н — от чистого пола помещения до оси изделия, у декора — до центра.
2. Красные цепочки — привязки электроточек и выводов: по горизонтали от угла чистовых стен, по вертикали от чистого пола, до оси изделия; звенья короче 3 мм на листе вынесены во второй ярус (ближняя к стене цепочка).
3. У знака электроточки: марка (Р — розетка, S — выключатель, Св — светильник, ЭВ — вывод кабеля), ×N — число постов в рамке, гр. — группа щита, Н — высота оси от чистого пола, мм; группы по клавишам выключателя — на листе выключателей.
4. Схема мебели, приборов и декора не является технической документацией для производства мебели; габариты — по паспортам изделий.
5. Двери скрытого монтажа — полотно в плоскости стены, отделка стены по полотну, плинтус прерывается у короба (узел — на листе узлов).

1000 мм · печать 1:1

Изм.	Кол.уч	Лист	№ док.	Подп.	Дата
Разраб.		Кырлан А.С.			19.10.26
Пров.					
ГИП					
Н. контр.					
Утв.					

ГД-2026-012-АИ

Дом 120 м²

Общая площадь 147,36* м² · * размеры приняты, не замерены (реестр — л. 6, К-1)

Дизайн-проект интерьера

Стадия	Лист	Листов
РП	111	130

Развёртки стен А, Б, В. Гардеробная (пом. 8)

М 1:40

Кырлан Александр Сергеевич

выпуск 19.10.2026 № 53e4f7ddae · стр. 117 из 160

Развёртка стены Г. Гардеробная (пом. 8)

Гардеробная (пом. 8) · вид изнутри помещения · размеры в мм, отметки в м

ПРЕДВАРИТЕЛЬНО · не для производства работ · открыто пунктов: 6 (реестр — л. 6)

Развёртка стены Г

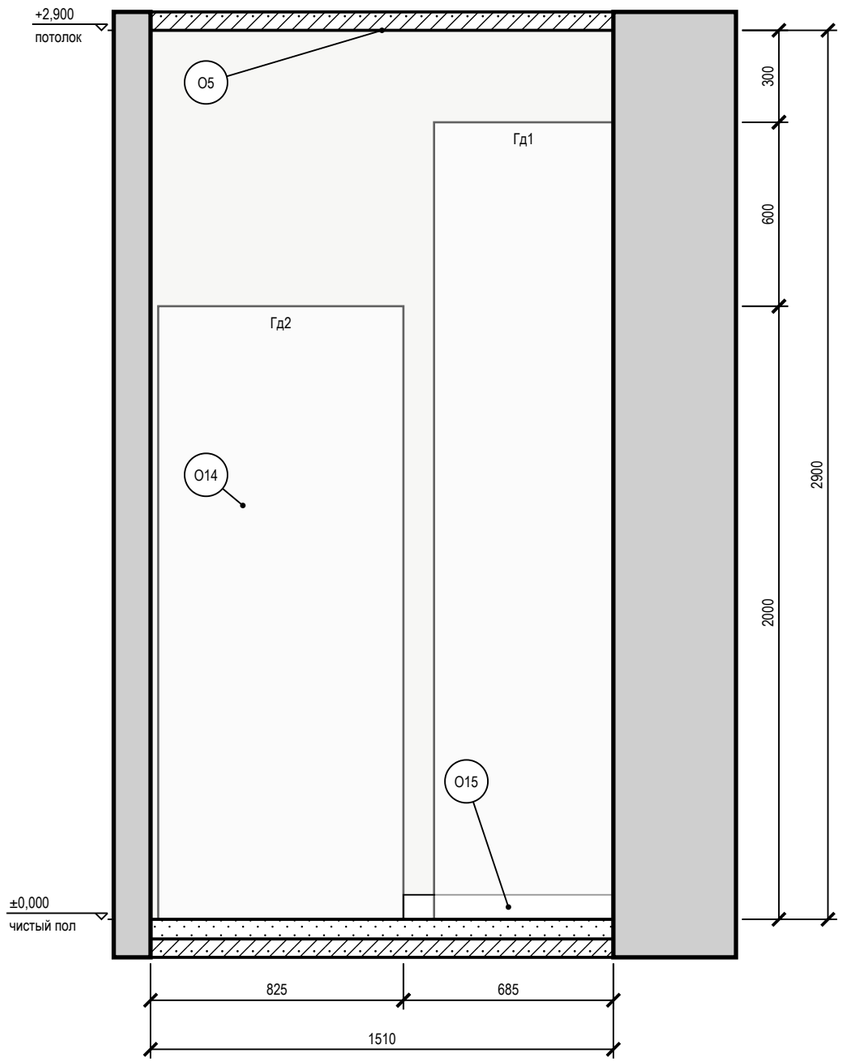

Схема развёрток (М 1:100)

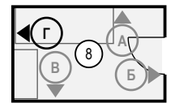

Условные обозначения

- привязки точек и выводов от угла и от пола, мм
- мебель и приборы — фасад по расстановке (условно)
- стены и перекрытия в сечении
- окраска: тон — цвет по коду производителя (условно)
- О1 — марка отделки по реестру отделки альбома
- А — марка развёртки: буква стены, стрелка — взгляд

Ведомость отделки (на листе)

Марка	Поверхность	Материал, изделие	Цвет, код	Кол.
О5	потолок	окраска, Tikkurila Anti-Reflex 2, глубокоматовая, подготовка Q3	Little Greene No. 222 «Loft White»	3,8 м²
О14	стены	окраска, Tikkurila Harmony, матовая, подготовка Q3	Little Greene No. 222 «Loft White»	4,4 м²
О15	плинтус	плинтус МДФ, h 80 мм, аналог: плинтус МДФ под покраску 80×16	Little Greene No. 222 «Loft White»	0,7 м

Допущения и предложения на листе

Основа листа: взаимное расположение помещений, контур дома 9600 × 8000 и раскладка этажей подобраны проектировщиком под габариты помещений брифа; обмер и проект АР — задание (К-1); высота потолка 2900 мм — по брифу, не замерена; перекрытие 330 мм и отметка 2-го этажа +3,230 приняты; проект КР — задание (К-2); наружные стены 400 мм, перегородки 120 мм приняты (в брифе толщин нет) (К-1); разрешённая мощность 15 кВт принята по типовым ТУ для частного дома (К-4).
См. лист открытых вопросов (лист 6, записи К-1, К-2, К-4).

Примечания

1. Развёртки — вид на стену изнутри помещения, по часовой стрелке; расположение — на схеме листа и на листе 94; размеры — в мм по чистовым поверхностям; отметки — в м от ±0,000; высоты Н — от чистого пола помещения до оси изделия, у декора — до центра.
2. Красные цепочки — привязки электроточек и выводов: по горизонтали от угла чистовых стен, по вертикали от чистого пола, до оси изделия; звенья короче 3 мм на листе вынесены во второй ярус (ближняя к стене цепочка).
3. У знака электроточки: марка (Р — розетка, S — выключатель, Св — светильник, ЭВ — вывод кабеля), ×N — число постов в рамке, гр. — группа щита, Н — высота оси от чистого пола, мм; группы по клавишам выключателя — на листе выключателей.
4. Схема мебели, приборов и декора не является технической документацией для производства мебели; габариты — по паспортам изделий.

1000 мм · печать 1:1

Изм.	Кол.уч	Лист	№ док.	Подп.	Дата
Разраб.		Кырлан А.С.			19.10.26
Пров.					
ГИП					
Н. контр.					
Утв.					

ГД-2026-012-АИ

Дом 120 м²

Общая площадь 147,36* м² · * размеры приняты, не замерены (реестр — л. 6, К-1)

Дизайн-проект интерьера

Стадия	Лист	Листов
РП	112	130

Развёртка стены Г. Гардеробная (пом. 8)

М 1:20

Кырлан Александр Сергеевич

выпуск 19.10.2026 № 53e4f7ddae · стр. 118 из 160

Развёртки стен. Кладовая (пом. 9)

Кладовая (пом. 9) · вид изнутри помещения · размеры в мм, отметки в м

ПРЕДВАРИТЕЛЬНО · не для производства работ · открыто пунктов: 6 (реестр — л. 6)

Развёртка стены Б

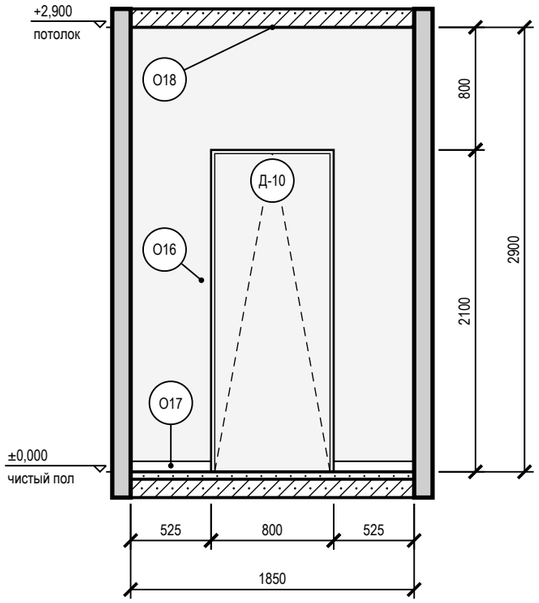

Развёртка стены В

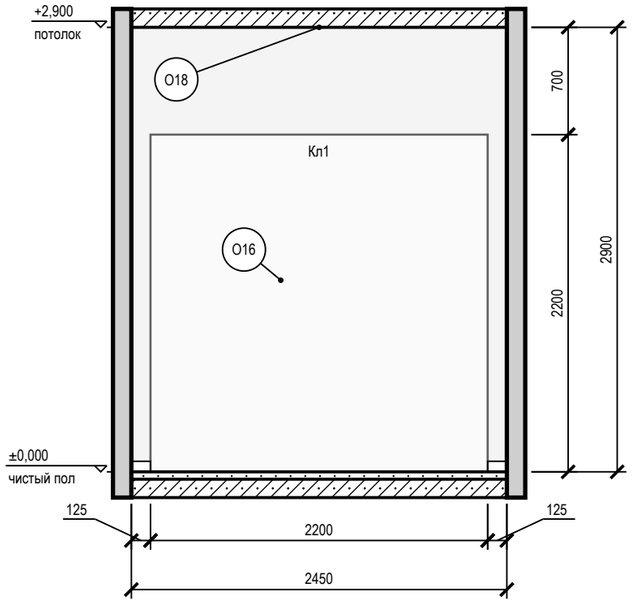

Развёртка стены Г

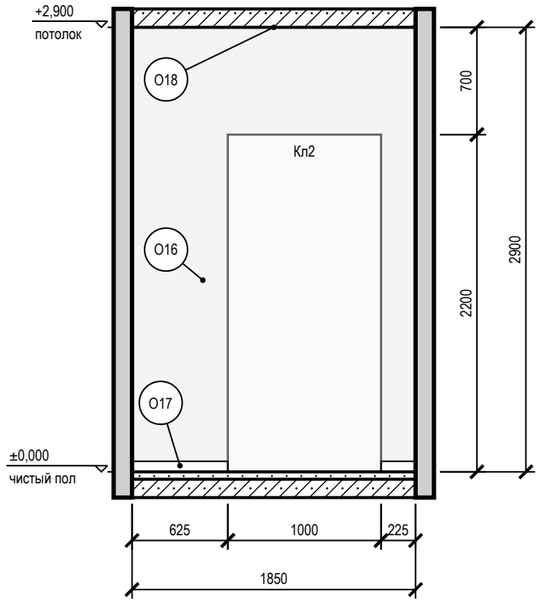

Условные обозначения

- привязки точек и выводов от угла и от пола, мм
- мебель и приборы — фасад по расстановке (условно)
- дверь скрытого монтажа: полотно в плоскости стены (узел — на листе узлов)
- стены и перекрытия в сечении
- О1 — марка отделки по реестру отделки альбома
- А — марка развёртки: буква стены, стрелка — взгляд

Схема развёрток (М 1:100)

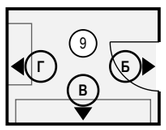

Ведомость отделки (на листе)

Марка	Поверхность	Материал, изделие	Цвет, код	Кол.
О16	стены	окраска, Tikkurila, матовая, подготовка Q3	NCS S 0502-Y	16,2 м²
О17	плинтус	плинтус МДФ, Orac Decor Contour (Luxxus), h 69 мм, SX165, шелковисто-матовая	NCS S 0300-N	2,1 м
О18	потолок	окраска, Tikkurila, глубокоматовая	NCS S 0300-N	4,7 м²

Допущения и предложения на листе

Основа листа: взаимное расположение помещений, контур дома 9600 × 8000 и раскладка этажей подобраны проектировщиком под габариты помещений брифа; обмер и проект АР — задание (К-1); высота потолка 2900 мм — по брифу, не замерена; перекрытие 330 мм и отметка 2-го этажа +3,230 приняты; проект КР — задание (К-2); наружные стены 400 мм, перегородки 120 мм приняты (в брифе толщин нет) (К-1); разрешённая мощность 15 кВт принята по типовым ТУ для частного дома (К-4).
См. лист открытых вопросов (лист 6, записи К-1, К-2, К-4).

Примечания

1. Развёртки — вид на стену изнутри помещения, по часовой стрелке; расположение — на схеме листа и на листе 94; размеры — в мм по чистовым поверхностям; отметки — в м от ±0,000; высоты Н — от чистого пола помещения до оси изделия, у декора — до центра.
2. Красные цепочки — привязки электроточек и выводов: по горизонтали от угла чистовых стен, по вертикали от чистого пола, до оси изделия; звенья короче 3 мм на листе вынесены во второй ярус (ближняя к стене цепочка).
3. У знака электроточки: марка (Р — розетка, S — выключатель, Св — светильник, ЭВ — вывод кабеля), ×N — число постов в рамке, гр. — группа щита, Н — высота оси от чистого пола, мм; группы по клавишам выключателя — на листе выключателей.
4. Схема мебели, приборов и декора не является технической документацией для производства мебели; габариты — по паспортам изделий.
5. Двери скрытого монтажа — полотно в плоскости стены, отделка стены по полотну, плинтус прерывается у короба (узел — на листе узлов).

1000 мм · печать 1:1

Изм.	Кол.уч	Лист	№ док.	Подп.	Дата
Разраб.		Кырлан А.С.			19.10.26
Пров.					
ГИП					
Н. контр.					
Утв.					

ГД-2026-012-АИ

Дом 120 м²

Общая площадь 147,36* м² · * размеры приняты, не замерены (реестр — л. 6, К-1)

Дизайн-проект интерьера

Стадия	Лист	Листов
РП	113	130

Развёртки стен. Кладовая (пом. 9)

М 1:40

Кырлан Александр Сергеевич

выпуск 19.10.2026 № 53e4f7ddae · стр. 119 из 160

Развёртки стен А, В. Холл второго этажа (пом. 10)

Холл второго этажа (пом. 10) · вид изнутри помещения · размеры в мм, отметки в м

ПРЕДВАРИТЕЛЬНО · не для производства работ · открыто пунктов: 6 (реестр — л. 6)

Развёртка стены А

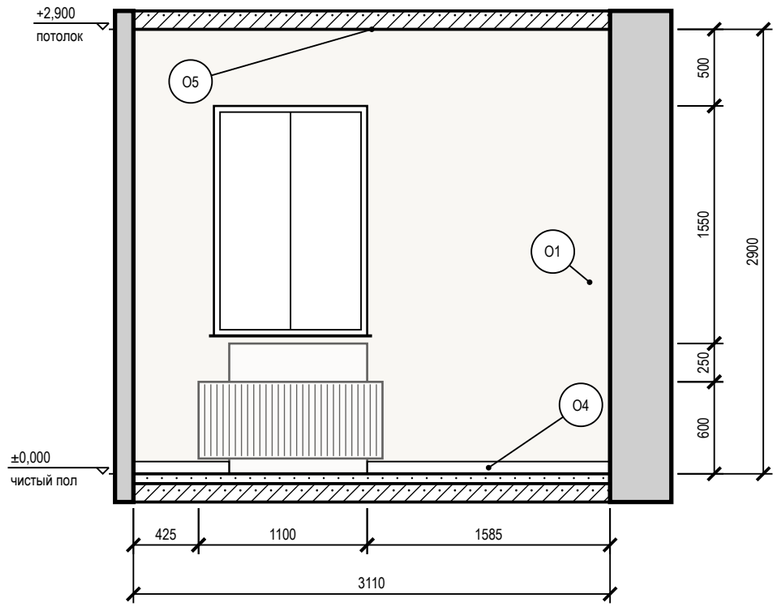

Развёртка стены В

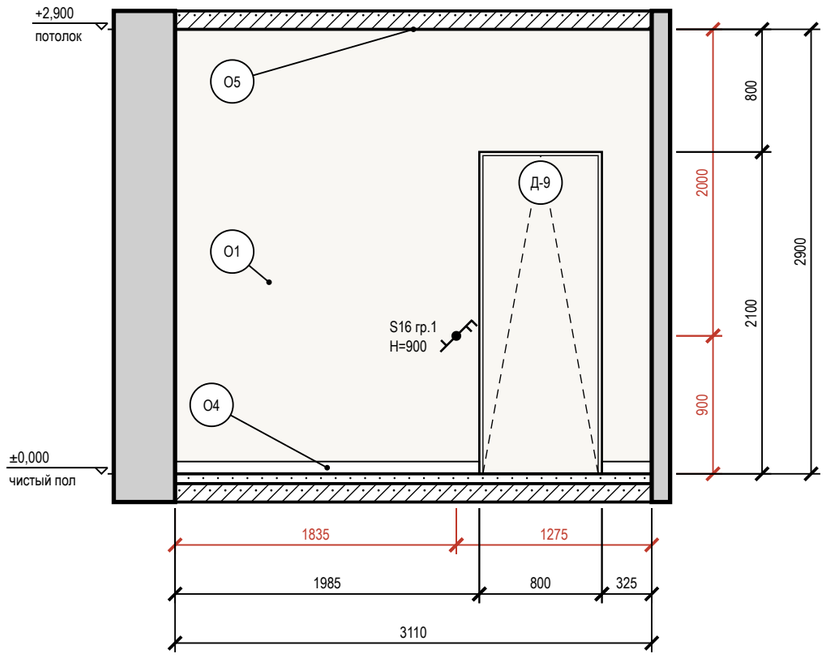

Условные обозначения

- выключатель одноклавишный
- выключатель двухклавишный (флажков — по числу клавиш)
- выключатель с проходной или перекрёстной клавишей (обратный флажок); тип клавиши — в подписи
- привязки точек и выводов от угла и от пола, мм
- мебель и приборы — фасад по расстановке (условно)
- дверь скрытого монтажа: полотно в плоскости стены (узел — на листе узлов)
- окно: проём, рама, подоконник
- радиатор отопления; марка — по плану отопления
- стены и перекрытия в сечении
- окраска: тон — цвет по коду производителя (условно)
- О1 — марка отделки по реестру отделки альбома
- А — марка развёртки: буква стены, стрелка — взгляд

Схема развёрток (М 1:100)

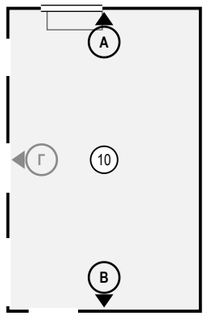

Ведомость отделки (на листе)

Марка	Поверхность	Материал, изделие	Цвет, код	Кол.
О1	стены	окраска, Farrow & Ball Modern Emulsion, матовая, подготовка Q3	Tikkurila G503 «Calla»	14,9 м²
О4	плинтус	плинтус МДФ, h 80 мм, аналог: плинтус МДФ под покраску 80×16	Tikkurila G503 «Calla»	4,5 м
О5	потолок	окраска, Tikkurila Anti-Reflex 2, глубокоматовая, подготовка Q3	Little Greene No. 222 «Loft White»	15,5 м²

Допущения и предложения на листе

Основа листа: взаимное расположение помещений, контур дома 9600 × 8000 и раскладка этажей подобраны проектировщиком под габариты помещений брифа; обмер и проект АР — задание (К-1); высота потолка 2900 мм — по брифу, не замерена; перекрытие 330 мм и отметка 2-го этажа +3,230 приняты; проект КР — задание (К-2); наружные стены 400 мм, перегородки 120 мм приняты (в брифе толщин нет) (К-1); разрешённая мощность 15 кВт принята по типовым ТУ для частного дома (К-4).
См. лист открытых вопросов (лист 6, записи К-1, К-2, К-4).

Примечания

1. Развёртки — вид на стену изнутри помещения, по часовой стрелке; расположение — на схеме листа и на листе 94; размеры — в мм по чистовым поверхностям; отметки — в м от ±0,000; высоты Н — от чистого пола помещения до оси изделия, у декора — до центра.
2. Красные цепочки — привязки электроточек и выводов: по горизонтали от угла чистовых стен, по вертикали от чистого пола, до оси изделия; звенья короче 3 мм на листе вынесены во второй ярус (ближняя к стене цепочка).
3. У знака электроточки: марка (Р — розетка, S — выключатель, Св — светильник, ЭВ — вывод кабеля), ×N — число постов в рамке, гр. — группа щита, Н — высота оси от чистого пола, мм; группы по клавишам выключателя — на листе выключателей.
4. Схема мебели, приборов и декора не является технической документацией для производства мебели; габариты — по паспортам изделий.
5. Двери скрытого монтажа — полотно в плоскости стены, отделка стены по полотну, плинтус прерывается у короба (узел — на листе узлов).

1000 мм · печать 1:1

Изм.	Кол.уч	Лист	№ док.	Подп.	Дата
Разраб.		Кырлан А.С.			19.10.26
Пров.					
ГИП					
Н. контр.					
Утв.					

ГД-2026-012-АИ

Дом 120 м²

Общая площадь 147,36* м² · * размеры приняты, не замерены (реестр — л. 6, К-1)

Дизайн-проект интерьера

Стадия	Лист	Листов
РП	114	130

Развёртки стен А, В. Холл второго этажа (пом. 10)

М 1:40

Кырлан Александр Сергеевич

выпуск 19.10.2026 № 536f7ddae · стр. 120 из 160

Развёртка стены Г. Холл второго этажа (пом. 10)

Холл второго этажа (пом. 10) · вид изнутри помещения · размеры в мм, отметки в м

ПРЕДВАРИТЕЛЬНО · не для производства работ · открыто пунктов: 6 (реестр — л. 6)

Развёртка стены Г

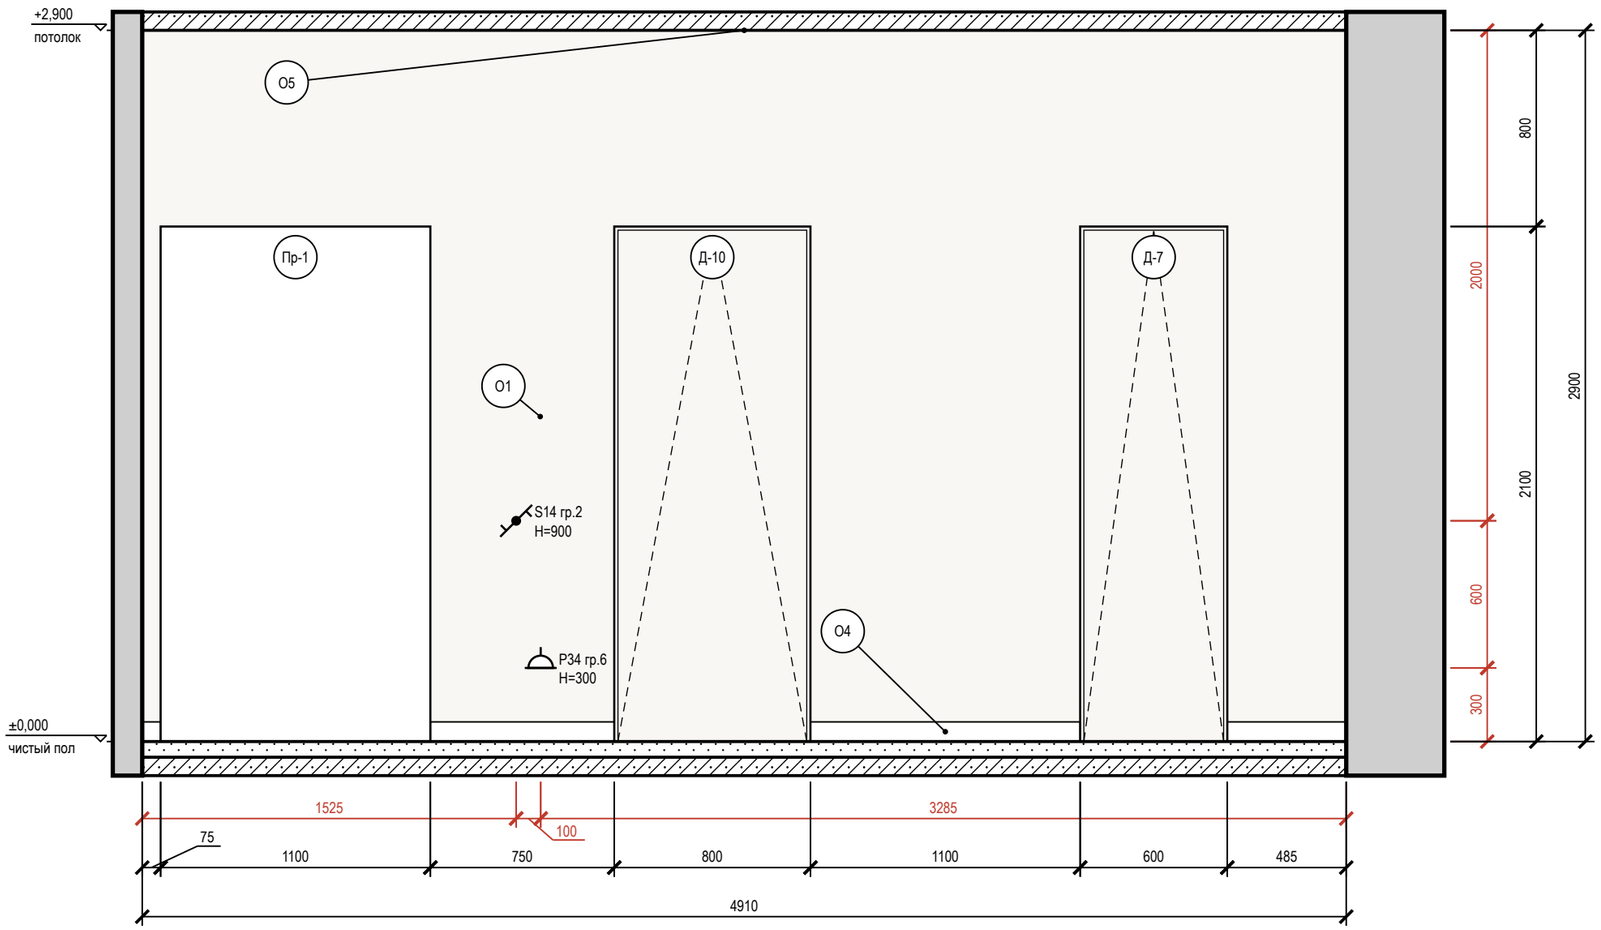

Схема развёрток (М 1:100)

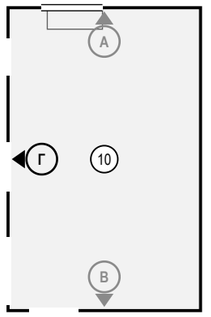

Условные обозначения

- розетка с заземляющим контактом; у знака — марка, ×N постов в рамке, гр. — группа щита, Н — высота оси, мм
- выключатель одноклавишный
- выключатель с проходной или перекрёстной клавишей (обратный флажок); тип клавиши — в подписи
- привязки точек и выводов от угла и от пола, мм
- мебель и приборы — фасад по расстановке (условно)
- дверь скрытого монтажа: полотно в плоскости стены (узел — на листе узлов)
- дверной проём; марка двери — в кружке
- стены и перекрытия в сечении
- окраска: тон — цвет по коду производителя (условно)
- О1 — марка отделки по реестру отделки альбома
- А — марка развёртки: буква стены, стрелка — взгляд

Ведомость отделки (на листе)

Марка	Поверхность	Материал, изделие	Цвет, код	Кол.
О1	стены	окраска, Farrow & Ball Modern Emulsion, матовая, подготовка Q3	Tikkurila G503 «Calla»	9 м²
О4	плинтус	плинтус МДФ, h 80 мм, аналог: плинтус МДФ под покраску 80×16	Tikkurila G503 «Calla»	2,4 м
О5	потолок	окраска, Tikkurila Anti-Reflex 2, глубокоматовая, подготовка Q3	Little Greene No. 222 «Loft White»	15,5 м²

Примечания

1. Развёртки — вид на стену изнутри помещения, по часовой стрелке; расположение — на схеме листа и на листе 94; размеры — в мм по чистовым поверхностям; отметки — в м от ±0,000; высоты Н — от чистого пола помещения до оси изделия, у декора — до центра.
2. Красные цепочки — привязки электроточек и выводов: по горизонтали от угла чистовых стен, по вертикали от чистого пола, до оси изделия; звенья короче 3 мм на листе вынесены во второй ярус (ближняя к стене цепочка).
3. У знака электроточки: марка (Р — розетка, S — выключатель, Св — светильник, ЭВ — вывод кабеля), ×N — число постов в рамке, гр. — группа щита, Н — высота оси от чистого пола, мм; группы по клавишам выключателя — на листе выключателей.
4. Схема мебели, приборов и декора не является технической документацией для производства мебели; габариты — по паспортам изделий.
5. Двери скрытого монтажа — полотно в плоскости стены, отделка стены по полотну, плинтус прерывается у короба (узел — на листе узлов).

1000 мм · печать 1:1

Допущения и предложения на листе

Основа листа: взаимное расположение помещений, контур дома 9600 × 8000 и раскладка этажей подобраны проектировщиком под габариты помещений брифа; обмер и проект АР — задание (К-1); высота потолка 2900 мм — по брифу, не замерена; перекрытие 330 мм и отметка 2-го этажа +3,230 приняты; проект КР — задание (К-2); наружные стены 400 мм, перегородки 120 мм приняты (в брифе толщин нет) (К-1); разрешённая мощность 15 кВт принята по типовым ТУ для частного дома (К-4).
См. лист открытых вопросов (лист 6, записи К-1, К-2, К-4).

Изм.	Кол.уч	Лист	№ док.	Подп.	Дата
Разраб.		Кырлан А.С.			19.10.26
Пров.					
ГИП					
Н. контр.					
Утв.					

ГД-2026-012-АИ

Дом 120 м²

Общая площадь 147,36* м² · * размеры приняты, не замерены (реестр — л. 6, К-1)

Дизайн-проект интерьера	Стадия	Лист	Листов
	РП	115	130

Развёртка стены Г. Холл второго этажа (пом. 10)

М 1:25

Кырлан Александр Сергеевич

выпуск 19.10.2026 № 53e4f7ddae · стр. 121 из 160

Развёртки стен. Коридор второго этажа (пом. 11)

Коридор второго этажа (пом. 11) · вид изнутри помещения · размеры в мм, отметки в м

ПРЕДВАРИТЕЛЬНО · не для производства работ · открыто пунктов: 6 (реестр — л. 6)

Развёртка стены А

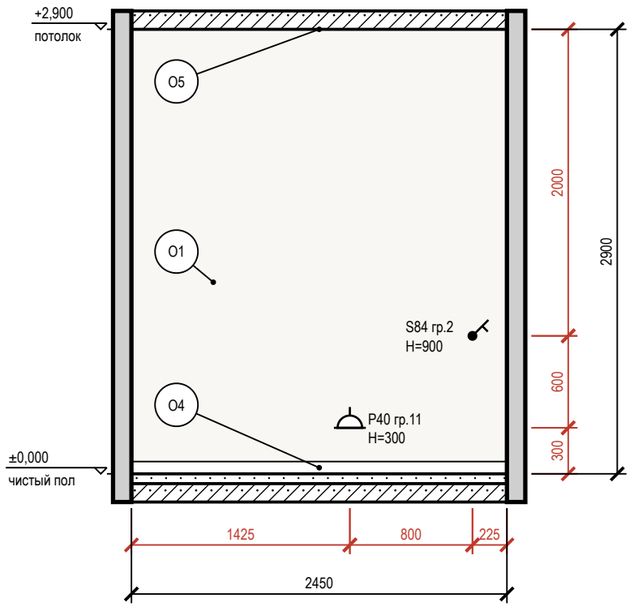

Развёртка стены В

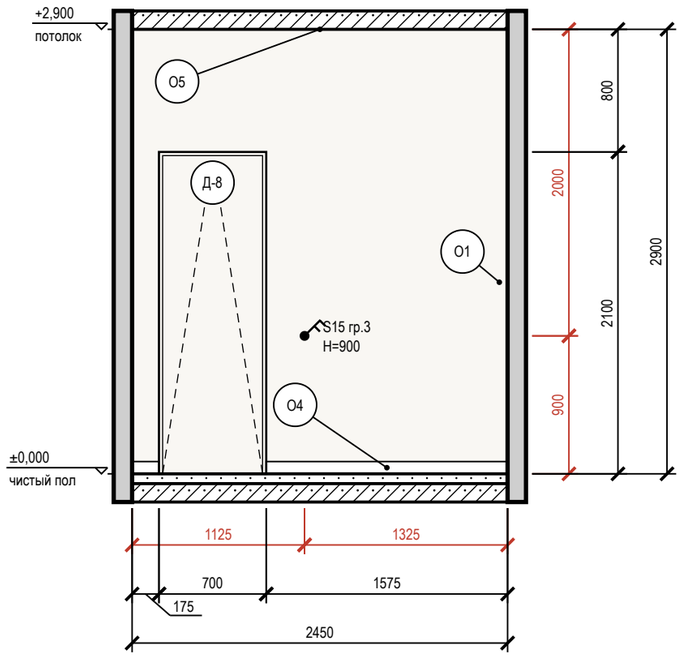

Развёртка стены Г

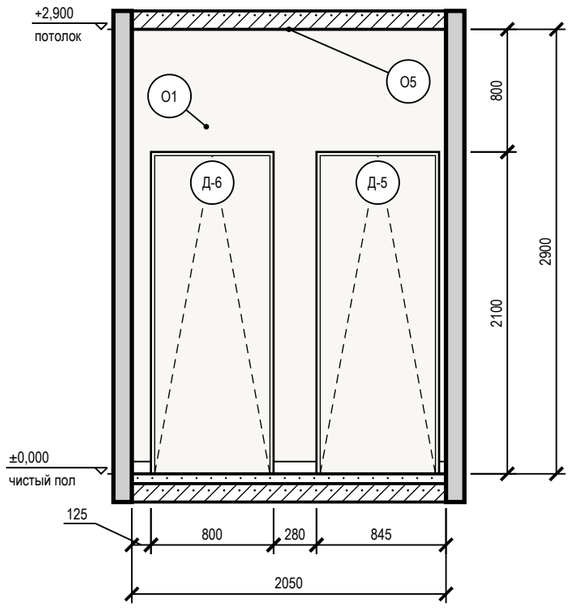

Схема развёрток (М 1:100)

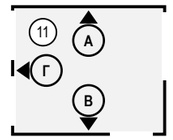

Условные обозначения

- розетка с заземляющим контактом; у знака — марка, ×N постов в рамке, гр. — группа щита, Н — высота оси, мм
- выключатель одноклавишный
- выключатель двухклавишный (флажков — по числу клавиш)
- привязки точек и выводов от угла и от пола, мм
- мебель и приборы — фасад по расстановке (условно)
- дверь скрытого монтажа: полотно в плоскости стены (узел — на листе узлов)
- стены и перекрытия в сечении
- окраска: тон — цвет по коду производителя (условно)
- О1 — марка отделки по реестру отделки альбома
- А — марка развёртки: буква стены, стрелка — взгляд

Ведомость отделки (на листе)

Марка	Поверхность	Материал, изделие	Цвет, код	Кол.
О1	стены	окраска, Farrow & Ball Modern Emulsion, матовая, подготовка Q3	Tikkurila G503 «Calla»	15,3 м²
О4	плинтус	плинтус МДФ, h 80 мм, аналог: плинтус МДФ под покраску 80×16	Tikkurila G503 «Calla»	4,7 м
О5	потолок	окраска, Tikkurila Anti-Reflex 2, глубокоматовая, подготовка Q3	Little Greene No. 222 «Loft White»	5,2 м²

Допущения и предложения на листе

Основа листа: взаимное расположение помещений, контур дома 9600 × 8000 и раскладка этажей подобраны проектировщиком под габариты помещений брифа; обмер и проект АР — задание (К-1); высота потолка 2900 мм — по брифу, не замерена; перекрытие 330 мм и отметка 2-го этажа +3,230 приняты; проект КР — задание (К-2); наружные стены 400 мм, перегородки 120 мм приняты (в брифе толщин нет) (К-1); разрешённая мощность 15 кВт принята по типовым ТУ для частного дома (К-4).
См. лист открытых вопросов (лист 6, записи К-1, К-2, К-4).

Примечания

1. Развёртки — вид на стену изнутри помещения, по часовой стрелке; расположение — на схеме листа и на листе 94; размеры — в мм по чистовым поверхностям; отметки — в м от ±0,000; высоты Н — от чистого пола помещения до оси изделия, у декора — до центра.
2. Красные цепочки — привязки электроточек и выводов: по горизонтали от угла чистовых стен, по вертикали от чистого пола, до оси изделия; звенья короче 3 мм на листе вынесены во второй ярус (ближняя к стене цепочка).
3. У знака электроточки: марка (Р — розетка, S — выключатель, Св — светильник, ЭВ — вывод кабеля), ×N — число постов в рамке, гр. — группа щита, Н — высота оси от чистого пола, мм; группы по клавишам выключателя — на листе выключателей.
4. Схема мебели, приборов и декора не является технической документацией для производства мебели; габариты — по паспортам изделий.
5. Двери скрытого монтажа — полотно в плоскости стены, отделка стены по полотну, плинтус прерывается у короба (узел — на листе узлов).

1000 мм · печать 1:1

Изм.	Кол.уч	Лист	№ док.	Подп.	Дата
Разраб.		Кырлан А.С.			19.10.26
Пров.					
ГИП					
Н. контр.					
Утв.					

ГД-2026-012-АИ

Дом 120 м²

Общая площадь 147,36* м² · * размеры приняты, не замерены (реестр — л. 6, К-1)

Дизайн-проект интерьера

Стадия	Лист	Листов
РП	116	130

Развёртки стен. Коридор второго этажа (пом. 11)

М 1:40

Кырлан Александр Сергеевич

выпуск 19.10.2026 № 536a4f7ddae · стр. 122 из 160

Развёртки стен А, Б. Детская вторая (пом. 12)

Детская вторая (пом. 12) · вид изнутри помещения · размеры в мм, отметки в м

ПРЕДВАРИТЕЛЬНО · не для производства работ · открыто пунктов: 6 (реестр — л. 6)

Развёртка стены А

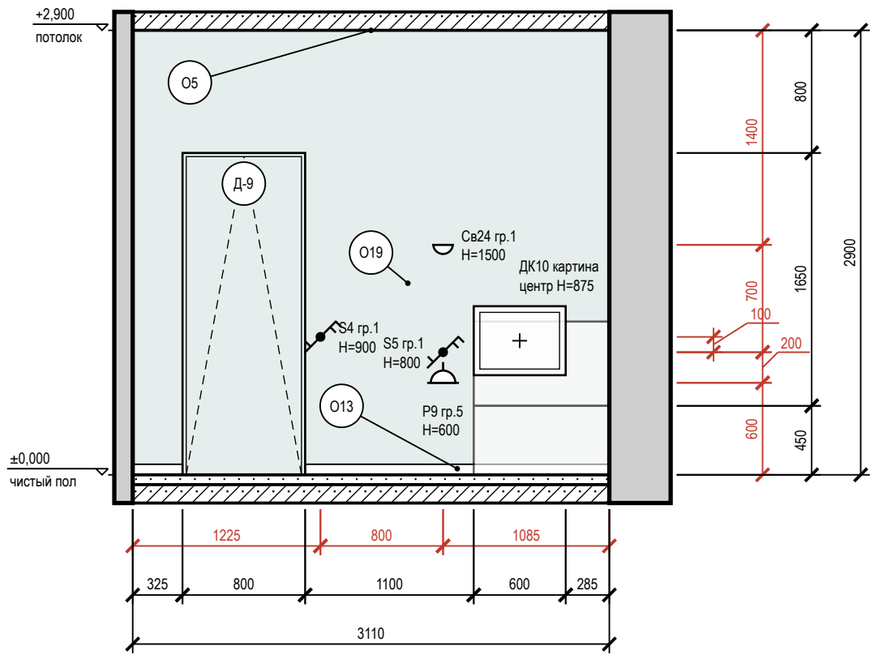

Развёртка стены Б

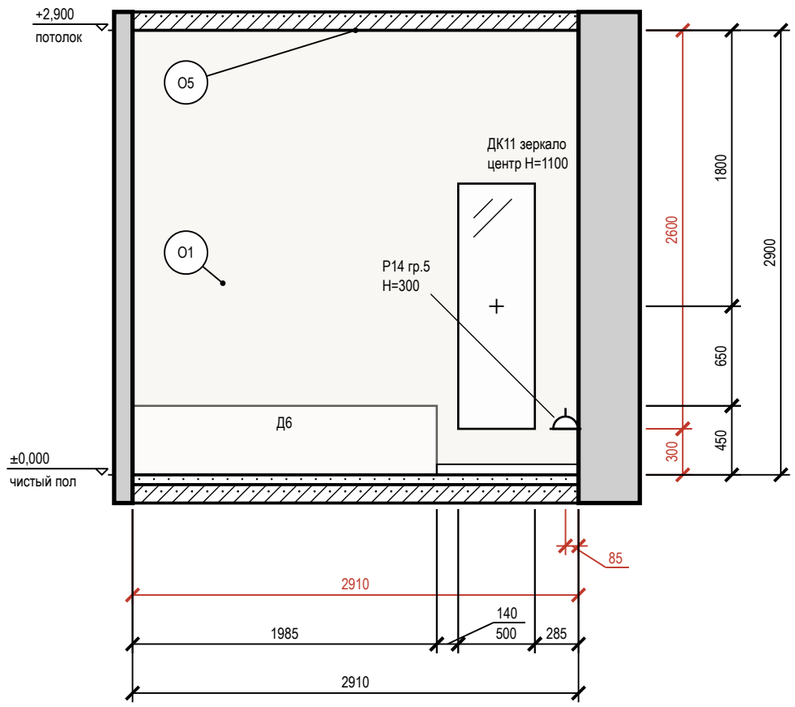

Условные обозначения

- розетка с заземляющим контактом; у знака — марка, ×N постов в рамке, гр. — группа щита, H — высота оси, мм
- выключатель одноклавишный
- выключатель двухклавишный (флажков — по числу клавиш)
- выключатель с проходной или перекрёстной клавишей (обратный флажок); тип клавиши — в подписи
- светильник настенный (бра), H — высота оси
- привязки точек и выводов от угла и от пола, мм
- мебель и приборы — фасад по расстановке (условно)
- картина (декор): марка Д, крест — центр, H — высота центра, мм
- зеркало: марка Д, крест — центр, H — высота центра, мм
- дверь скрытого монтажа: полотно в плоскости стены (узел — на листе узлов)
- стены и перекрытия в сечении
- окраска: тон — цвет по коду производителя (условно)
- О1 — марка отделки по реестру отделки альбома
- А — марка развёртки: буква стены, стрелка — взгляд

Схема развёрток (М 1:100)

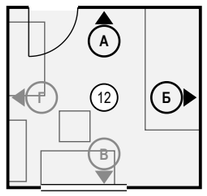

Ведомость отделки (на листе)

Марка	Поверхность	Материал, изделие	Цвет, код	Кол.
О1	стены	окраска, Farrow & Ball Modern Emulsion, матовая, подготовка Q3	Tikkurila G503 «Calla»	8,4 м²
О5	потолок	окраска, Tikkurila Anti-Reflex 2, глубокоматовая, подготовка Q3	Little Greene No. 222 «Loft White»	9,2 м²
О13	плинтус	плинтус МДФ, Orac Decor Contour (Luxxus), h 69 мм, SX165	Tikkurila G503 «Calla»	3,2 м
О19	акцентная стена	окраска, Farrow & Ball Modern Emulsion, матовая, подготовка Q3	Tikkurila H440 «H440 Wave — бирюзово-голубая вода»	7,3 м²

Допущения и предложения на листе

Основа листа: взаимное расположение помещений, контур дома 9600 × 8000 и раскладка этажей подобраны проектировщиком под габариты помещений брифа; обмер и проект АР — задание (К-1); высота потолка 2900 мм — по брифу, не замерена; перекрытие 330 мм и отметка 2-го этажа +3,230 приняты; проект КР — задание (К-2); наружные стены 400 мм, перегородки 120 мм приняты (в брифе толщин нет) (К-1); разрешённая мощность 15 кВт принята по типовым ТУ для частного дома (К-4).
См. лист открытых вопросов (лист 6, записи К-1, К-2, К-4).

Примечания

1. Развёртки — вид на стену изнутри помещения, по часовой стрелке; расположение — на схеме листа и на листе 94; размеры — в мм по чистовым поверхностям; отметки — в м от ±0,000; высоты H — от чистого пола помещения до оси изделия, у декора — до центра.
2. Красные цепочки — привязки электроточек и выводов: по горизонтали от угла чистовых стен, по вертикали от чистого пола, до оси изделия; звенья короче 3 мм на листе вынесены во второй ярус (ближняя к стене цепочка).
3. У знака электроточки: марка (Р — розетка, S — выключатель, Св — светильник, ЭВ — вывод кабеля), ×N — число постов в рамке, гр. — группа щита, H — высота оси от чистого пола, мм; группы по клавишам выключателя — на листе выключателей.
4. Схема мебели, приборов и декора не является технической документацией для производства мебели; габариты — по паспортам изделий.
5. Картины и зеркала крепить к основанию по паспорту изделия (закладные и анкеры — в перечне скрытых работ); крест — ось центра предмета.
6. Двери скрытого монтажа — полотно в плоскости стены, отделка стены по полотну, плинтус прерывается у короба (узел — на листе узлов).

1000 мм · печать 1:1

Изм.	Кол.уч	Лист	№ док.	Подп.	Дата
Разраб.		Кырлан А.С.			19.10.26
Пров.					
ГИП					
Н. контр.					
Утв.					

ГД-2026-012-АИ

Дом 120 м²

Общая площадь 147,36* м² · * размеры приняты, не замерены (реестр — л. 6, К-1)

Дизайн-проект интерьера

Стадия	Лист	Листов
РП	117	130

Развёртки стен А, Б. Детская вторая (пом. 12)

М 1:40

Кырлан Александр Сергеевич

выпуск 19.10.2026 № 536a1f7ddae · стр. 123 из 160

Развёртки стен В, Г. Детская вторая (пом. 12)

Детская вторая (пом. 12) · вид изнутри помещения · размеры в мм, отметки в м

ПРЕДВАРИТЕЛЬНО · не для производства работ · открыто пунктов: 6 (реестр — л. 6)

Развёртка стены В

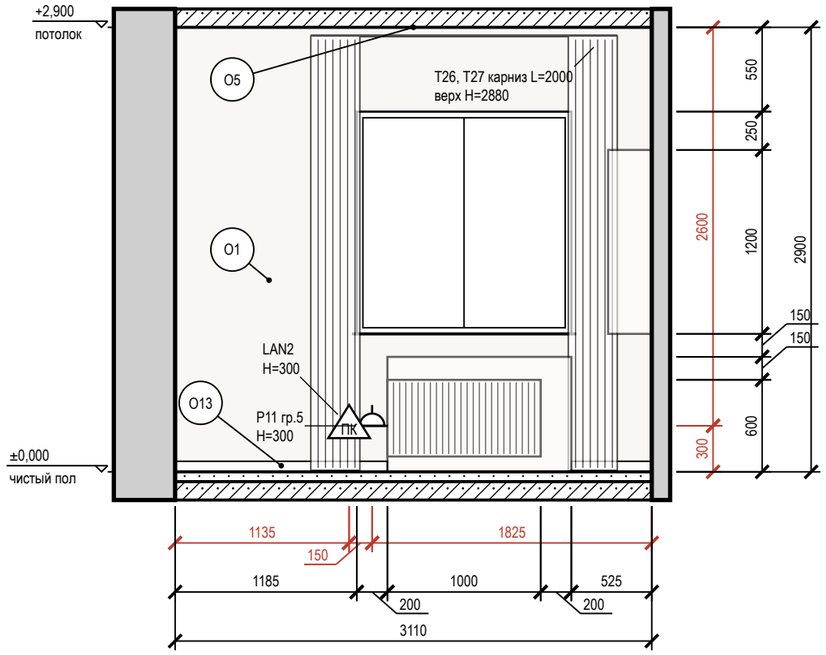

Развёртка стены Г

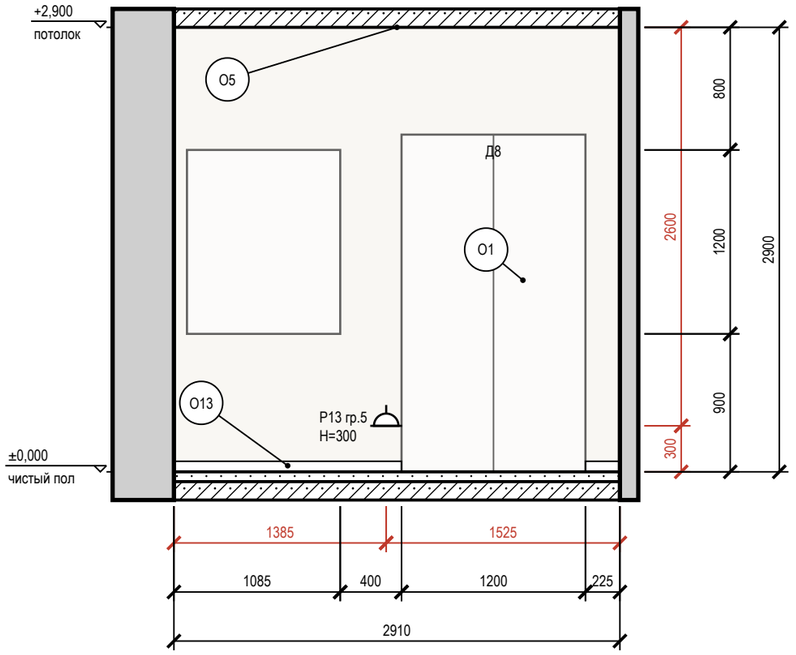

Условные обозначения

- розетка с заземляющим контактом; у знака — марка, ×N постов в рамке, гр. — группа щита, H — высота оси, мм
- ПК — розетка компьютерная RJ45
- привязки точек и выводов от угла и от пола, мм
- мебель и приборы — фасад по расстановке (условно)
- карниз (шина) и шторы в собранном виде: марка T, длина L, верх H
- окно: проём, рама, подоконник
- радиатор отопления; марка — по плану отопления
- стены и перекрытия в сечении
- окраска: тон — цвет по коду производителя (условно)
- О1 — марка отделки по реестру отделки альбома
- А — марка развёртки: буква стены, стрелка — взгляд

Схема развёрток (М 1:100)

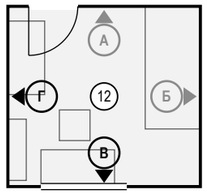

Ведомость отделки (на листе)

Марка	Поверхность	Материал, изделие	Цвет, код	Кол.
О1	стены	окраска, Farrow & Ball Modern Emulsion, матовая, подготовка Q3	Tikkurila G503 «Calla»	15,4 м²
О5	потолок	окраска, Tikkurila Anti-Reflex 2, глубокоматовая, подготовка Q3	Little Greene No. 222 «Loft White»	9,2 м²
О13	плинтус	плинтус МДФ, Orac Decor Contour (Luxxus), h 69 мм, SX165	Tikkurila G503 «Calla»	3,6 м

Допущения и предложения на листе

Основа листа: взаимное расположение помещений, контур дома 9600 × 8000 и раскладка этажей подобраны проектировщиком под габариты помещений брифа; обмер и проект АР — задание (К-1); высота потолка 2900 мм — по брифу, не замерена; перекрытие 330 мм и отметка 2-го этажа +3,230 приняты; проект КР — задание (К-2); наружные стены 400 мм, перегородки 120 мм приняты (в брифе толщин нет) (К-1); разрешённая мощность 15 кВт принята по типовым ТУ для частного дома (К-4).
См. лист открытых вопросов (лист 6, записи К-1, К-2, К-4).

Примечания

1. Развёртки — вид на стену изнутри помещения, по часовой стрелке; расположение — на схеме листа и на листе 94; размеры — в мм по чистовым поверхностям; отметки — в м от ±0,000; высоты H — от чистого пола помещения до оси изделия, у декора — до центра.
2. Красные цепочки — привязки электроточек и выводов: по горизонтали от угла чистовых стен, по вертикали от чистого пола, до оси изделия; звенья короче 3 мм на листе вынесены во второй ярус (ближняя к стене цепочка).
3. У знака электроточки: марка (Р — розетка, S — выключатель, Св — светильник, ЭВ — вывод кабеля), ×N — число постов в рамке, гр. — группа щита, H — высота оси от чистого пола, мм; группы по клавишам выключателя — на листе выключателей.
4. Схема мебели, приборов и декора не является технической документацией для производства мебели; габариты — по паспортам изделий.
5. Карнизы (шины) — по ведомости текстиля декоратора; длина L и верх H — по развёртке, крепление — до окраски потолка.

1000 мм · печать 1:1

Изм.	Кол.уч	Лист	№ док.	Подп.	Дата
Разраб.		Кырлан А.С.			19.10.26
Пров.					
ГИП					
Н. контр.					
Утв.					

ГД-2026-012-АИ

Дом 120 м²

Общая площадь 147,36* м² · * размеры приняты, не замерены (реестр — л. 6, К-1)

Дизайн-проект интерьера

Стадия	Лист	Листов
РП	118	130

Развёртки стен В, Г. Детская вторая (пом. 12)

М 1:40

Кырлан Александр Сергеевич

выпуск 19.10.2026 № 536417ddae · стр. 124 из 160

Развёртка стены А. Санузел второго этажа (пом. 13)

Санузел второго этажа (пом. 13) · вид изнутри помещения · размеры в мм, отметки в м

ПРЕДВАРИТЕЛЬНО · не для производства работ · открыто пунктов: 6 (реестр — л. 6)

Развёртка стены А

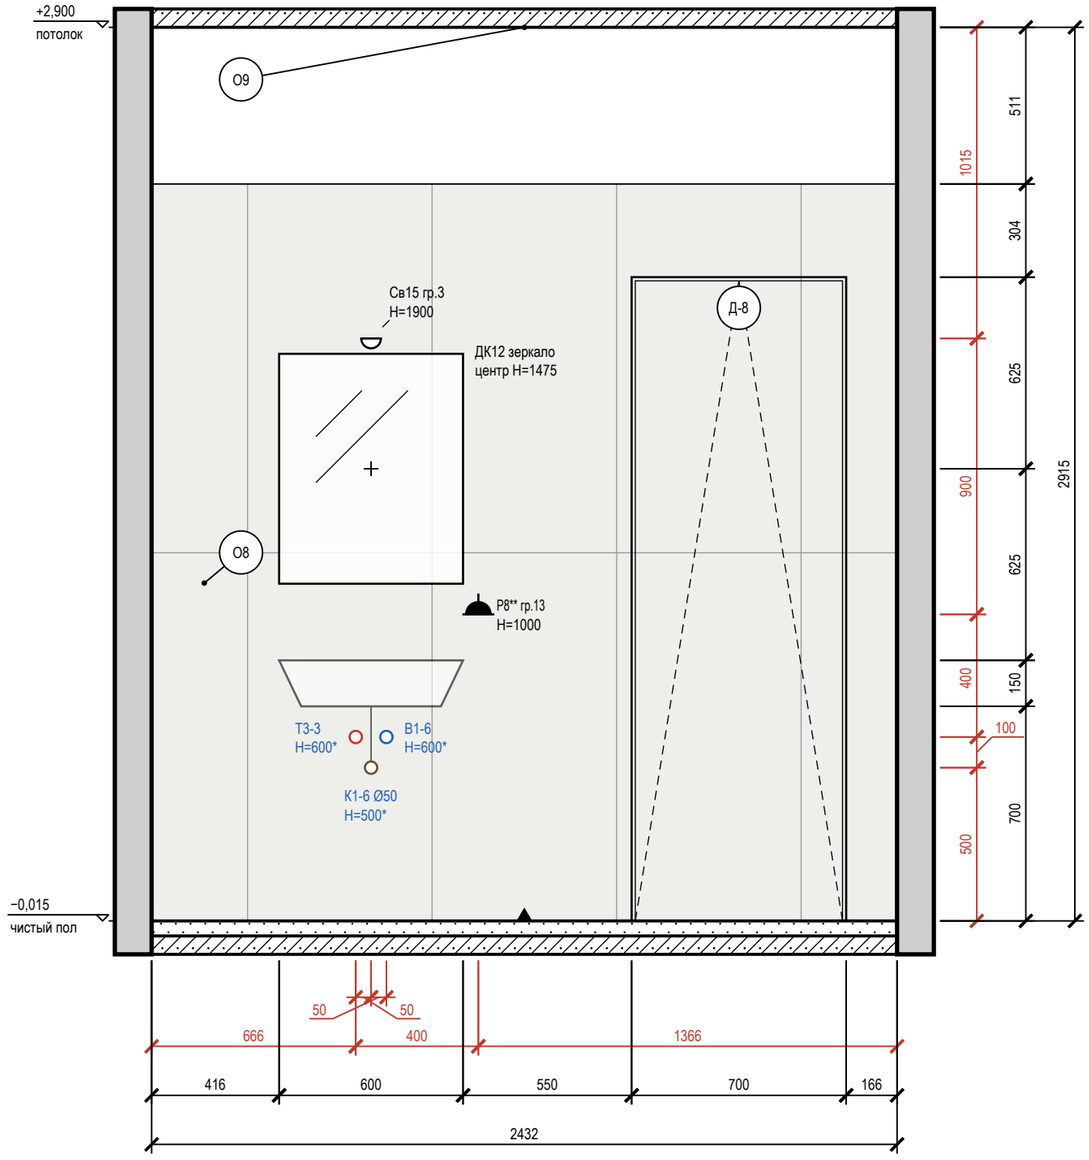

Схема развёрток (М 1:100)

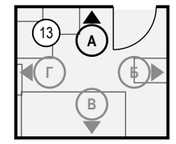

Допущения и предложения на листе

Основа листа: взаимное расположение помещений, контур дома 9600 × 8000 и раскладка этажей подобраны проектировщиком под габариты помещений брифа; обмер и проект АР — задание (К-1); высота потолка 2900 мм — по брифу, не замерена; перекрытие 330 мм и отметка 2-го этажа +3,230 приняты; проект КР — задание (К-2); наружные стены 400 мм, перегородки 120 мм приняты (в брифе толщин нет) (К-1); разрешённая мощность 15 кВт принята по типовым ТУ для частного дома (К-4).

Знак «**» — предложение проектировщика, заказчиком не утверждено (согласовать с заказчиком): записи в реестре нет: Р8 — по образцу: Р7, Р8 и Р33 на высоте 1000 мм — верхний предел нормы (ПУЭ, п. 6.6.30, не выше 1 м); флаг решения снят.

См. лист открытых вопросов (лист 6, записи К-1, К-2, К-4).

Условные обозначения

- розетка влагозащищённая IP44
- светильник настенный (бра), H — высота оси
- вывод В1 (код — в ведомости привязок)
- вывод Т3 (код — в ведомости привязок)
- вывод К1 (код — в ведомости привязок)
- привязки точек и выводов от угла и от пола, мм
- мебель и приборы — фасад по расстановке (условно)
- зеркало: марка Д, крест — центр, H — высота центра, мм
- дверь скрытого монтажа: полотно в плоскости стены (узел — на листе узлов)
- стены и перекрытия в сечении
- плитка: сетка швов по формату, ▲ — ось старта
- О1 — марка отделки по реестру отделки альбома
- А — марка развёртки: буква стены, стрелка — взгляд

Ведомость отделки (на листе)

Марка	Поверхность	Материал, изделие	Цвет, код	Кол.
О8	стены	облицовка плиткой, Atlas Concorde Marvel Travertine, 600×1200×9 мм, A8UZ, затирка CG2WA	Atlas Concorde A8UZ «Marvel Travertine»	4,4 м²
О9	потолок	окраска, Tikkurila Luja 7, матовая, подготовка Q3	Little Greene No. 222 «Loft White»	5,3 м²

Примечания

1. Развёртки — вид на стену изнутри помещения, по часовой стрелке; расположение — на схеме листа и на листе 94; размеры — в мм по чистовым поверхностям; отметки — в м от ±0,000; высоты H — от чистого пола помещения до оси изделия, у декора — до центра.
2. Красные цепочки — привязки электроточек и выводов: по горизонтали от угла чистовых стен, по вертикали от чистого пола, до оси изделия; звенья короче 3 мм на листе вынесены во второй ярус (ближняя к стене цепочка).
3. У знака электроточки: марка (Р — розетка, S — выключатель, Св — светильник, ЭВ — вывод кабеля), ×N — число постов в рамке, гр. — группа щита, H — высота оси от чистого пола, мм; группы по клавишам выключателя — на листе выключателей.
4. Схема мебели, приборов и декора не является технической документацией для производства мебели; габариты — по паспортам изделий (* — высота не задана в проекте, показана по типовому изделию).
5. Выводы ВК — коды и высоты по листу выводов сантехники; * — высота принята по типовой практике монтажа, окончательно — по паспорту прибора.
6. Облицовка — по сетке швов 2 мм, раскладка от оси стены (треугольник у пола), целые ряды от пола; подрезки — по листу раскладки плитки.
7. Гидроизоляция в 2 слоя, заход на стены 200 мм — до облицовки, с актом скрытых работ и тестом проливом (узел — на листе узлов).
8. Картины и зеркала крепить к основанию по паспорту изделия (закладные и анкеры — в перечне скрытых работ); крест — ось центра предмета.
9. Двери скрытого монтажа — полотно в плоскости стены, отделка стены по полотну, плинтус прерывается у короба (узел — на листе узлов).

1000 мм · печать 1:1

Изм.	Кол.уч	Лист	№ док.	Подп.	Дата
Разраб.		Кырлан А.С.			19.10.26
Пров.					
ГИП					
Н. контр.					
Утв.					

ГД-2026-012-АИ

Дом 120 м²

Общая площадь 147,36* м² · * размеры приняты, не замерены (реестр — л. 6, К-1)

Дизайн-проект интерьера	Стадия	Лист	Листов
	РП	119	130

Развёртка стены А. Санузел второго этажа (пом. 13)

М 1:20

Кырлан Александр Сергеевич

Развёртка стены Б. Санузел второго этажа (пом. 13)

Санузел второго этажа (пом. 13) · вид изнутри помещения · размеры в мм, отметки в м

ПРЕДВАРИТЕЛЬНО · не для производства работ · открыто пунктов: 6 (реестр — л. 6)

Развёртка стены Б

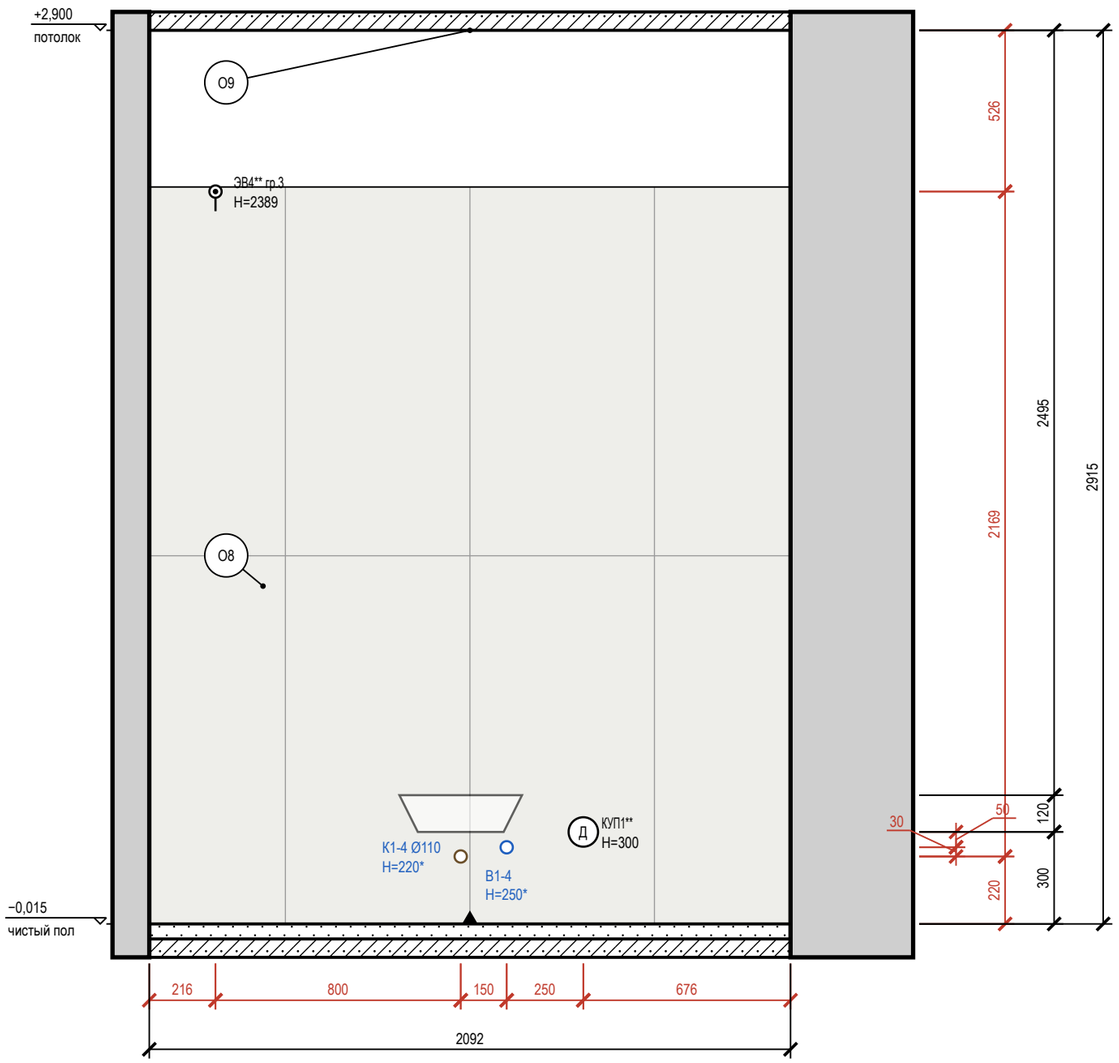

Схема развёрток (М 1:100)

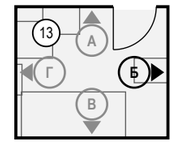

Условные обозначения

- вывод кабеля для подключения прибора (без розетки), марка ЭВ
- вывод В1 (код — в ведомости привязок)
- вывод К1 (код — в ведомости привязок)
- привязки точек и выводов от угла и от пола, мм
- мебель и приборы — фасад по расстановке (условно)
- стены и перекрытия в сечении
- плитка: сетка швов по формату, ▲ — ось старта
- О1 — марка отделки по реестру отделки альбома
- А — марка развёртки: буква стены, стрелка — взгляд

Ведомость отделки (на листе)

Марка	Поверхность	Материал, изделие	Цвет, код	Кол.
О8	стены	облицовка плиткой, Atlas Concorde Marvel Travertine, 600×1200×9 мм, A8UZ, затирка CG2WA	Atlas Concorde A8UZ «Marvel Travertine»	5 м²
О9	потолок	окраска, Tikkurila Luja 7, матовая, подготовка Q3	Little Greene No. 222 «Loft White»	5,3 м²

Допущения и предложения на листе

Основа листа: взаимное расположение помещений, контур дома 9600 × 8000 и раскладка этажей подобраны проектировщиком под габариты помещений брифа; обмер и проект АР — задание (К-1); высота потолка 2900 мм — по брифу, не замерена; перекрытие 330 мм и отметка 2-го этажа +3,230 приняты; проект КР — задание (К-2); наружные стены 400 мм, перегородки 120 мм приняты (в брифе толщин нет) (К-1); разрешённая мощность 15 кВт принята по типовым ТУ для частного дома (К-4).

Знак «**» — предложение проектировщика, заказчиком не утверждено (согласовать с заказчиком): записи в реестре нет: ЭВ4, КУП1 — по образцу: Добавлены выводы к вентиляторам: ЭВ4 (ВР1, ванная) и ЭВ5 (ВР3, санузел 2) — группа 3, высота 2389 мм, включение с основным светом, таймер выбега в вентиляторе; и коробки уравнивания потенциалов КУП1 (ванная) и КУП2 (санузел 2) — высота 300 мм, у входа, вне зон 0–2, проводник от шины PE щита ЩК, сече.

См. лист открытых вопросов (лист 6, записи К-1, К-2, К-4).

Примечания

1. Развёртки — вид на стену изнутри помещения, по часовой стрелке; расположение — на схеме листа и на листе 94; размеры — в мм по чистовым поверхностям; отметки — в м от ±0,000; высоты Н — от чистого пола помещения до оси изделия, у декора — до центра.
2. Красные цепочки — привязки электроточек и выводов: по горизонтали от угла чистовых стен, по вертикали от чистого пола, до оси изделия; звенья короче 3 мм на листе вынесены во второй ярус (ближняя к стене цепочка).
3. У знака электроточки: марка (Р — розетка, S — выключатель, Св — светильник, ЭВ — вывод кабеля), ×N — число постов в рамке, гр. — группа щита, Н — высота оси от чистого пола, мм; группы по клавишам выключателя — на листе выключателей.
4. Схема мебели, приборов и декора не является технической документацией для производства мебели; габариты — по паспортам изделий (* — высота не задана в проекте, показана по типовому изделию).
5. Выводы ВК — коды и высоты по листу выводов сантехники; * — высота принята по типовой практике монтажа, окончательно — по паспорту прибора.
6. Облицовка — по сетке швов 2 мм, раскладка от оси стены (треугольник у пола), целые ряды от пола; подрезки — по листу раскладки плитки.
7. Гидроизоляция в 2 слоя, заход на стены 200 мм — до облицовки, с актом скрытых работ и тестом проливом (узел — на листе узлов).

1000 мм · печать 1:1

Изм.	Кол.уч	Лист	№ док.	Подп.	Дата
Разраб.		Кырлан А.С.			19.10.26
Пров.					
ГИП					
Н. контр.					
Утв.					

ГД-2026-012-АИ

Дом 120 м²

Общая площадь 147,36* м² · * размеры приняты, не замерены (реестр — л. 6, К-1)

Дизайн-проект интерьера	Стадия	Лист	Листов
	РП	120	130
Развёртка стены Б. Санузел второго этажа (пом. 13) М 1:20	**Кырлан Александр Сергеевич**		

выпуск 19.10.2026 № 536f7ddae · стр. 126 из 160

Развёртка стены В. Санузел второго этажа (пом. 13)

Санузел второго этажа (пом. 13) · вид изнутри помещения · размеры в мм, отметки в м

ПРЕДВАРИТЕЛЬНО · не для производства работ · открыто пунктов: 6 (реестр — л. 6)

Развёртка стены В

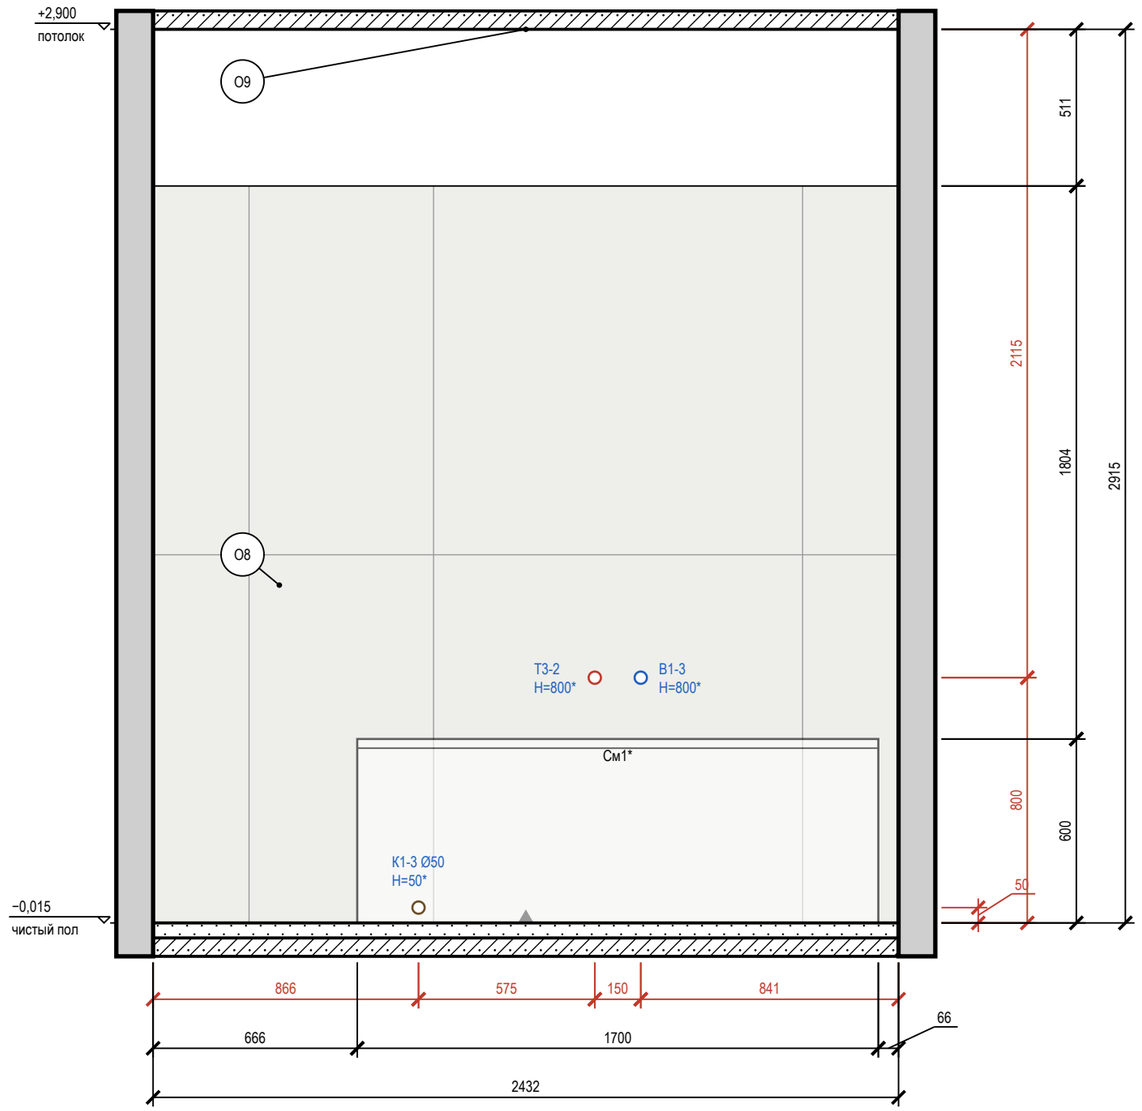

Схема развёрток (М 1:100)

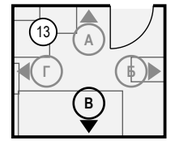

Условные обозначения

- вывод В1 (код — в ведомости привязок)
- вывод Т3 (код — в ведомости привязок)
- вывод К1 (код — в ведомости привязок)
- привязки точек и выводов от угла и от пола, мм
- мебель и приборы — фасад по расстановке (условно)
- стены и перекрытия в сечении
- плитка: сетка швов по формату, ▲ — ось старта
- О1 — марка отделки по реестру отделки альбома
- А — марка развёртки: буква стены, стрелка — взгляд

Ведомость отделки (на листе)

Марка	Поверхность	Материал, изделие	Цвет, код	Кол.
О8	стены	облицовка плиткой, Atlas Concorde Marvel Travertine, 600×1200×9 мм, А8UZ, затирка CG2WA	Atlas Concorde A8UZ «Marvel Travertine»	5,8 м²
О9	потолок	окраска, Tikkurila Luja 7, матовая, подготовка Q3	Little Greene No. 222 «Loft White»	5,3 м²

Допущения и предложения на листе

Основа листа: взаимное расположение помещений, контур дома 9600 × 8000 и раскладка этажей подобраны проектировщиком под габариты помещений брифа; обмер и проект АР — задание (К-1); высота потолка 2900 мм — по брифу, не замерена; перекрытие 330 мм и отметка 2-го этажа +3,230 приняты; проект КР — задание (К-2); наружные стены 400 мм, перегородки 120 мм приняты (в брифе толщин нет) (К-1); разрешённая мощность 15 кВт принята по типовым ТУ для частного дома (К-4).

См. лист открытых вопросов (лист 6, записи К-1, К-2, К-4).

Примечания

1. Развёртки — вид на стену изнутри помещения, по часовой стрелке; расположение — на схеме листа и на листе 94; размеры — в мм по чистовым поверхностям; отметки — в м от ±0,000; высоты Н — от чистого пола помещения до оси изделия, у декора — до центра.
2. Красные цепочки — привязки электроточек и выводов: по горизонтали от угла чистовых стен, по вертикали от чистого пола, до оси изделия; звенья короче 3 мм на листе вынесены во второй ярус (ближняя к стене цепочка).
3. У знака электроточки: марка (Р — розетка, S — выключатель, Св — светильник, ЭВ — вывод кабеля), ×N — число постов в рамке, гр. — группа щита, Н — высота оси от чистого пола, мм; группы по клавишам выключателя — на листе выключателей.
4. Схема мебели, приборов и декора не является технической документацией для производства мебели; габариты — по паспортам изделий (* — высота не задана в проекте, показана по типовому изделию).
5. Выводы ВК — коды и высоты по листу выводов сантехники; * — высота принята по типовой практике монтажа, окончательно — по паспорту прибора.
6. Облицовка — по сетке швов 2 мм, раскладка от оси стены (треугольник у пола), целые ряды от пола; подрезки — по листу раскладки плитки.
7. Гидроизоляция в 2 слоя, заход на стены 200 мм — до облицовки, с актом скрытых работ и тестом проливом (узел — на листе узлов).

1000 мм · печать 1:1

Изм.	Кол.уч	Лист	№ док.	Подп.	Дата
Разраб.		Кырлан А.С.			19.10.26
Пров.					
ГИП					
Н. контр.					
Утв.					

ГД-2026-012-АИ

Дом 120 м²

Общая площадь 147,36* м² · * размеры приняты, не замерены (реестр — л. 6, К-1)

Дизайн-проект интерьера

Стадия	Лист	Листов
РП	121	130

Развёртка стены В. Санузел второго этажа (пом. 13)

М 1:20

Кырлан Александр Сергеевич

выпуск 19.10.2026 № 53e4f7ddae · стр. 127 из 160

Развёртка стены Г. Санузел второго этажа (пом. 13)

Санузел второго этажа (пом. 13) · вид изнутри помещения · размеры в мм, отметки в м

ПРЕДВАРИТЕЛЬНО · не для производства работ · открыто пунктов: 6 (реестр — л. 6)

Развёртка стены Г

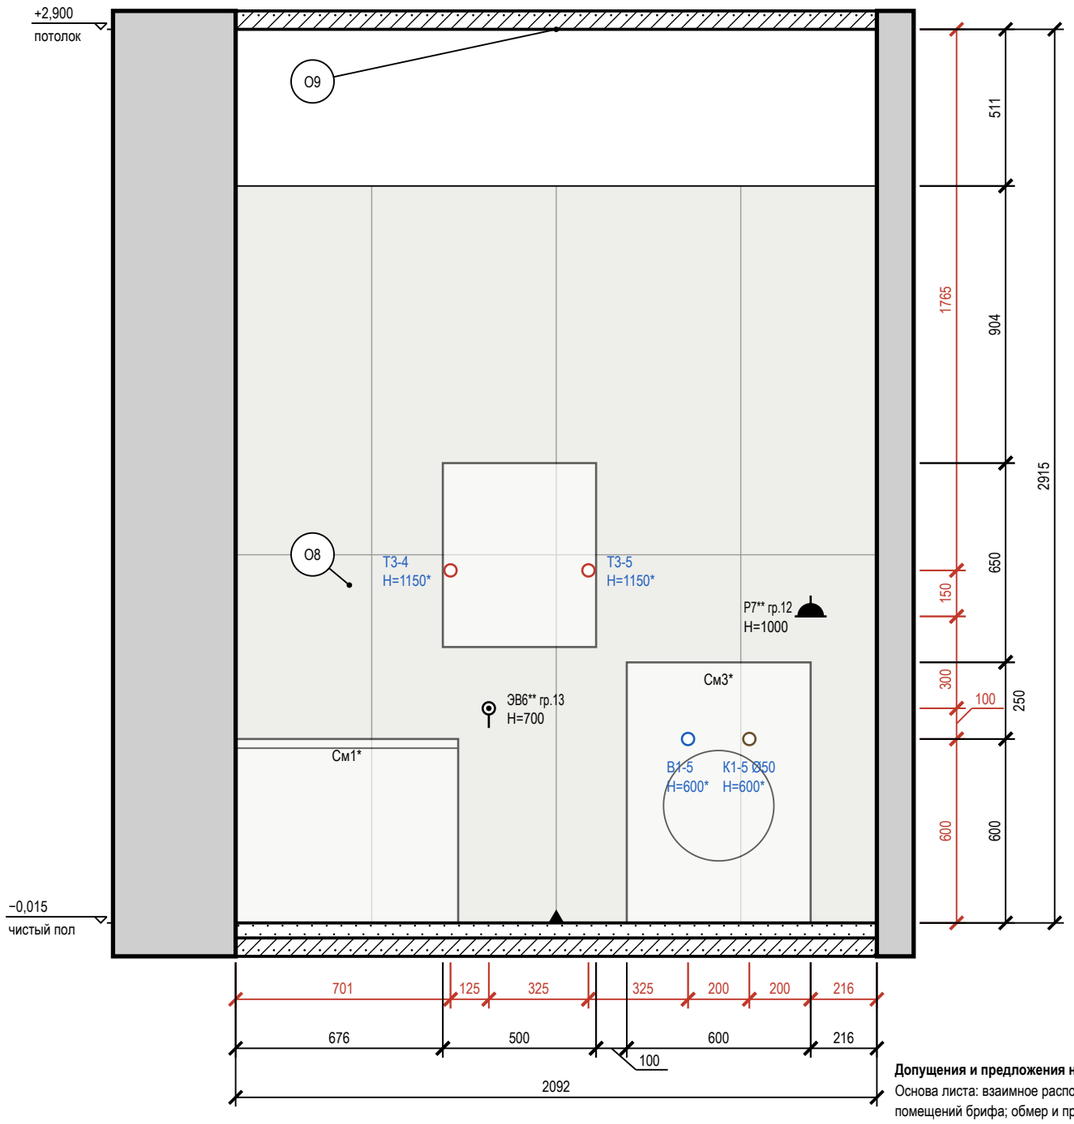

Схема развёрток (М 1:100)

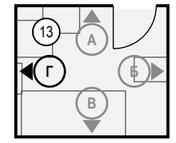

Условные обозначения

- розетка влагозащищённая IP44
- вывод кабеля для подключения прибора (без розетки), марка ЭВ
- вывод В1 (код — в ведомости привязок)
- вывод Т3 (код — в ведомости привязок)
- вывод К1 (код — в ведомости привязок)
- привязки точек и выводов от угла и от пола, мм
- мебель и приборы — фасад по расстановке (условно)
- стены и перекрытия в сечении
- плитка: сетка швов по формату, ▲ — ось старта
- О1 — марка отделки по реестру отделки альбома
- А — марка развёртки: буква стены, стрелка — взгляд

Ведомость отделки (на листе)

Марка	Поверхность	Материал, изделие	Цвет, код	Кол.
О8	стены	облицовка плиткой, Atlas Concorde Marvel Travertine, 600×1200×9 мм, A8UZ, затирка CG2WA	Atlas Concorde A8UZ «Marvel Travertine»	5 м²
О9	потолок	окраска, Tikkurila Luja 7, матовая, подготовка Q3	Little Greene No. 222 «Loft White»	5,3 м²

Допущения и предложения на листе

Основа листа: взаимное расположение помещений, контур дома 9600 × 8000 и раскладка этажей подобраны проектировщиком под габариты помещений брифа; обмер и проект АР — задание (К-1); высота потолка 2900 мм — по брифу, не замерена; перекрытие 330 мм и отметка 2-го этажа +3,230 приняты; проект КР — задание (К-2); наружные стены 400 мм, перегородки 120 мм приняты (в брифе толщин нет) (К-1); разрешённая мощность 15 кВт принята по типовым ТУ для частного дома (К-4).

Знак «**» — предложение проектировщика, заказчиком не утверждено (согласовать с заказчиком): записи в реестре нет: Р7 — по образцу: Р7, Р8 и Р33 на высоте 1000 мм — верхний предел нормы (ПУЭ, п. 6.6.30, не выше 1 м); флаг решения снят; ЭВ6 — по образцу: Добавлены электрические полотенцесушители IP44: П10 в ванной (480 мм, низ 900 мм) и П13 в санузле 2 (400 мм, низ 900 мм), выводы ЭВ6 и ЭВ7; мощность группы 13 — 2,4 кВт вместо 1,8 кВт.

См. лист открытых вопросов (лист 6, записи К-1, К-2, К-4).

Примечания

1. Развёртки — вид на стену изнутри помещения, по часовой стрелке; расположение — на схеме листа и на листе 94; размеры — в мм по чистовым поверхностям; отметки — в м от ±0,000; высоты Н — от чистого пола помещения до оси изделия, у декора — до центра.
2. Красные цепочки — привязки электроточек и выводов: по горизонтали от угла чистовых стен, по вертикали от чистого пола, до оси изделия; звенья короче 3 мм на листе вынесены во второй ярус (ближняя к стене цепочка).
3. У знака электроточки: марка (Р — розетка, S — выключатель, Св — светильник, ЭВ — вывод кабеля), ×N — число постов в рамке, гр. — группа щита, Н — высота оси от чистого пола, мм; группы по клавишам выключателя — на листе выключателей.
4. Схема мебели, приборов и декора не является технической документацией для производства мебели; габариты — по паспортам изделий (* — высота не задана в проекте, показана по типовому изделию).
5. Выводы ВК — коды и высоты по листу выводов сантехники; * — высота принята по типовой практике монтажа, окончательно — по паспорту прибора.
6. Облицовка — по сетке швов 2 мм, раскладка от оси стены (треугольник у пола), целые ряды от пола; подрезки — по листу раскладки плитки.
7. Гидроизоляция в 2 слоя, заход на стены 200 мм — до облицовки, с актом скрытых работ и тестом проливом (узел — на листе узлов).

1000 мм · печать 1:1

Изм.	Кол.уч	Лист	№ док.	Подп.	Дата
Разраб.		Кырлан А.С.			19.10.26
Пров.					
ГИП					
Н. контр.					
Утв.					

ГД-2026-012-АИ

Дом 120 м²

Общая площадь 147,36* м² · * размеры приняты, не замерены (реестр — л. 6, К-1)

Дизайн-проект интерьера

Стадия	Лист	Листов
РП	122	130

Развёртка стены Г. Санузел второго этажа (пом. 13)

М 1:20

Кырлан Александр Сергеевич

выпуск 19.10.2026 № 53e4f7ddae · стр. 128 из 160

Узлы

Пороги и стыки покрытий, скрытые двери, короба стояков, гидроизоляция, плинтус

1 Порог 15 мм: мокрая зона — жилое помещение (М 1:5)

Применение: двери Д-3, Д-8; места — лист 94

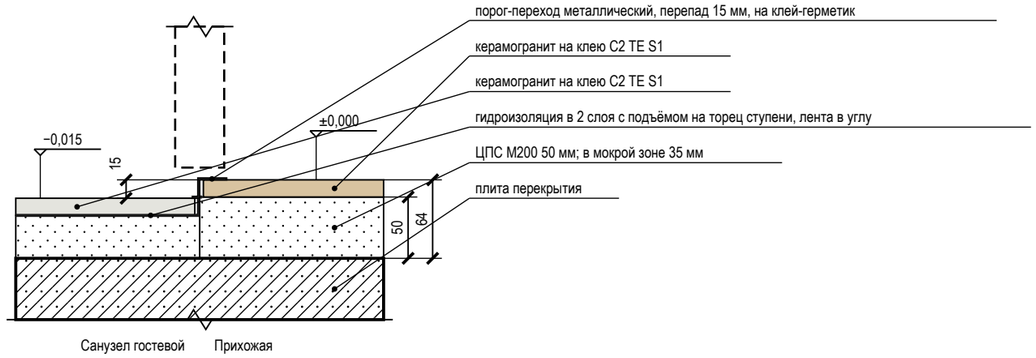

2 Дверь скрытого монтажа в плоскости стены, плинтус (М 1:5)

Применение: двери Д-1, Д-2, Д-3, Д-4, Д-5, Д-6, Д-7, Д-10, Д-9, Д-8; места — лист 94

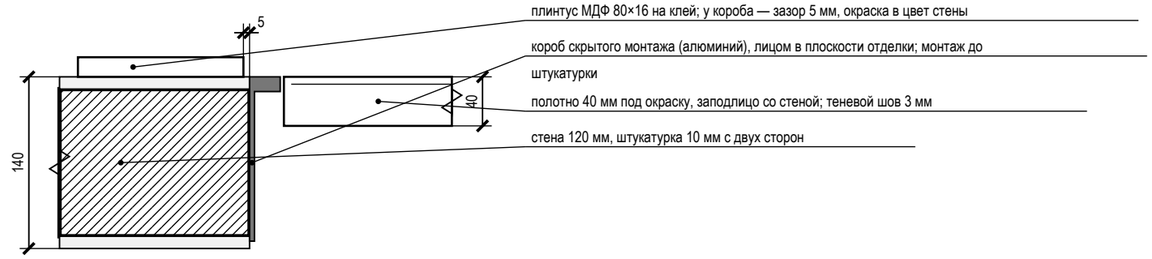

3 Короб стояков К1-1 с люком и звукоизоляцией (М 1:10)

Применение: пом. 4, 1; места — лист 94

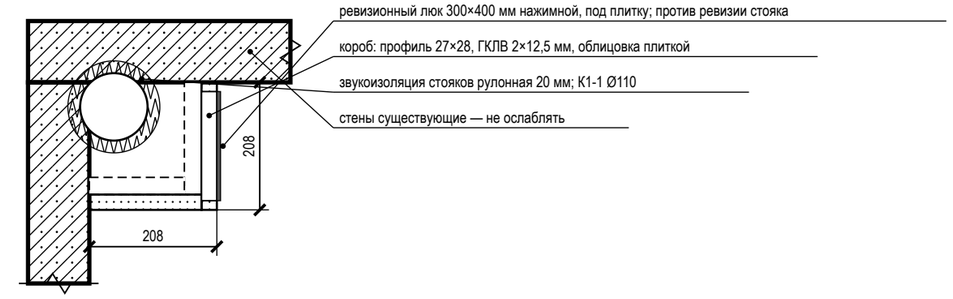

4 Гидроизоляция санузла: заход на стены 200 мм, примыкание ванны (М 1:20)

Применение: пом. 4, 13; места — лист 94

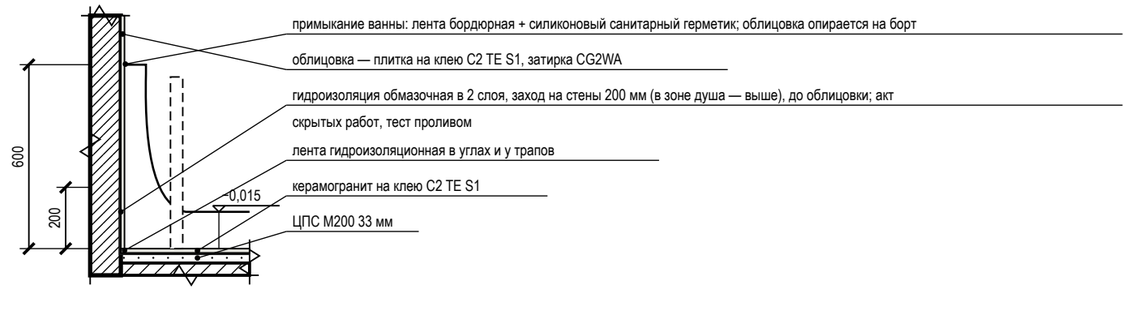

5 Плинтус МДФ 80×16 мм у окрашенной стены (М 1:10)

Применение: пом. 1, 2, 3, 5, 6, 7, 8, 9, 10, 11, 12; места — лист 94

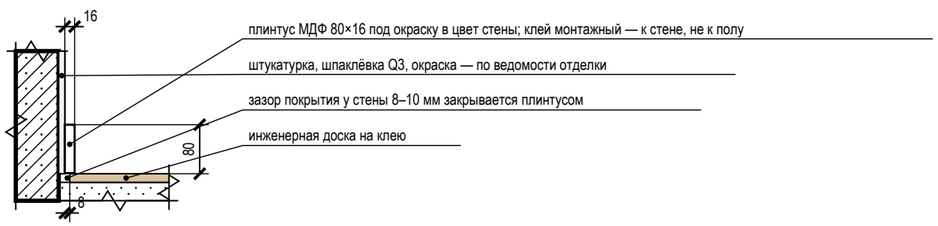

Условные обозначения

- железобетон (плита, стены)
- кладка, перегородка
- стяжка, раствор
- гипсокартон ГКЛВ
- звукоизоляция, эластичный заполнитель
- плитка, керамогранит на клею
- инженерная доска (покрытие пола)
- металлический профиль (порог, Т-профиль, короб двери)
- гидроизоляция (обмазочная, лента)

Примечания

1. Узлы — типовые решения проекта для мест, отмеченных выносками на листе схемы расположения развёрток и узлов; размеры — в мм, отметки — в м от ±0,000.
2. Узлы с гидроизоляцией, закладными и коробами скрытого монтажа принимаются по актам скрытых работ до закрытия отделкой; гидроизоляция — после теста проливом (24 ч).
3. Марки изделий (порог, Т-профиль, короб скрытой двери, люк) — по спецификациям; замена — на аналог с теми же габаритами по согласованию с автором проекта.

Допущения и предложения на листе

Основа листа: взаимное расположение помещений, контур дома 9600 × 8000 и раскладка этажей подобраны проектировщиком под габариты помещений брифа; обмер и проект АР — задание (К-1); высота потолка 2900 мм — по брифу, не замерена; перекрытие 330 мм и отметка 2-го этажа +3,230 приняты; проект КР — задание (К-2); наружные стены 400 мм, перегородки 120 мм приняты (в брифе толщин нет) (К-1); разрешённая мощность 15 кВт принята по типовым ТУ для частного дома (К-4).
См. лист открытых вопросов (лист 6, записи К-1, К-2, К-4).

Изм.	Кол.уч	Лист	№ док.	Подп.	Дата
Разраб.		Кырлан А.С.			19.10.26
Пров.					
ГИП					
Н. контр.					
Утв.					

ГД-2026-012-АИ

Дом 120 м²

Общая площадь 147,36* м² · * размеры приняты, не замерены (реестр — л. 6, К-1)

Дизайн-проект интерьера

Стадия	Лист	Листов
РП	123	130

Узлы

М б/м

Кырлан Александр Сергеевич

выпуск 19.10.2026 № 53e4f7ddae · стр. 129 из 160

05

Смета

Кырлан Александр Сергеевич

выпуск 19.10.2026 · 53e4f7ddae · стр. 130 из 160

Ведомость объёмов работ

ПРЕДВАРИТЕЛЬНО · не для производства работ · открыто пунктов: 6 (реестр — л. 6)

Объёмы по помещениям от чертежа · площади в м², длины в м · формула, правило проёмов и источник в каждой строке

Ведомость объёмов работ по помещениям

Поз.	Наименование работ (материал, число слоёв)	Ед. изм.	Объём по помещениям (№ по экспликации)													Всего	Формула подсчёта	Правило проёмов	Источник	Цена за ед., ₽	Стоимость, ₽
			1	2	3	4	5	6	7	8	9	10	11	12	13						
1. Демонтаж и черновые работы																					
1	Демонтаж существующего покрытия пола до основания	м²	31,32	15,51	11,00	4,17	12,20	17,17	12,30	3,82	4,66	15,51	5,16	9,23	5,31	147,36	S пом.		л. 13–16	по КП	
2	Демонтаж существующей отделки стен до основания	м²	56,72	34,65	34,81	21,65	43,20	43,93	36,92	22,06	23,61	34,65	19,31	31,55	23,78	426,84	P × H − проёмы	за вычетом проёмов	л. 13–16	по КП	
3	Демонтаж существующей отделки потолка до основания	м²	31,32	15,51	11,00	4,17	12,20	17,17	12,30	3,82	4,66	15,51	5,16	9,23	5,31	147,36	S пом.		л. 13–16	по КП	
4	Демонтаж существующих дверных блоков	шт	1		1	1	2	1	1	1	1			1	1	11	по ведомости проёмов		л. 15–18	по КП	
5	Демонтаж существующих сантехприборов и электрооборудования (если есть)	компл															по факту на объекте		л. 15, 16	по КП	
6	Устройство стяжки: стяжка ЦПС М200, 50 мм	м²	31,37	15,82	11,05	4,24	12,54	17,22	12,35	3,86		15,82	5,36	9,28	5,40	144,31	S пом. + S в дверных проёмах (b × t/2)	проёмы добавлены	л. 58–61	530	76 484
7	Гидроизоляция обмазочная, 2 слоя: пол, стены на 200 мм, зоны замачивания	м²				5,45									12,32	17,77	пол + (P − двери) × h заведения + зоны замачивания		л. 54	450	7 997
8	Штукатурка стен по маякам, до 10 мм	м²	56,72	34,65	34,81	21,65	43,20	43,93	36,92	22,06		34,65	19,31	31,55	23,78	403,23	P × H − проёмы по обводу коробок − грани перегородок на ГКЛВ	за вычетом проёмов	л. 13, 14, 60, 61	530	213 712
9	Штукатурка оконных откосов шириной более 200 мм	м²	3,53	1,32	1,49			1,58	1,45			1,32		1,42		12,11	Σ (2h + b) × глубина откоса	откосы > 200 мм	л. 13, 14	540	6 539
Итого по разделу 1 — 304 732 ₽ (позиций 9, из них по КП 5); в сводную смету — л. 129, 130																					
2. Инженерные системы																					
10	Прокладка кабеля ВВГнг(A)-LS по группам щита: за потолком и в штробах стен (штробы — только после технического заключения, см. строку «Штробы в стенах»)	м														508,00	Σ длин групп щита		л. 36, 37	60	30 480
11	Прокладка слаботочной линии: Кабель домофона — тип по системе поставщика, отдельно от силовых	м														6,10	по лучам от ЩС**: 1 точ., запас 10 %		л. 40, 41	по КП	
12	Прокладка слаботочной линии: Кабель коаксиальный RG-6 (75 Ом) к розеткам ТВ, отдельно от силовых	м														16,70	по лучам от ЩС**: 1 точ., запас 10 %		л. 40, 41	по КП	
13	Прокладка слаботочной линии: Кабель U/UTP кат. 6 (LAN, Wi-Fi и камеры по PoE), отдельно от силовых	м														71,00	по лучам от ЩС**: 6 точ., запас 10 %		л. 40, 41	по КП	
14	Прокладка гофротрубы Ø20 для слаботочных линий, отдельно от силовых	м														84,40	по длине лучей без участков в канале плинтуса (≈ 90 %)		л. 40, 41	по КП	
15	Сборка слаботочного щита ЩС**: корпус, патч-панель, подключение линий и питания 220 В; коммутатор и точки доступа — оборудование заказчика	шт														1	один щит		л. 34, 35, 40, 41	по КП	
16	Электроточка: подрозетник в бетоне, розетка, выключатель, вывод	шт	24	3	7	3	8	9	7			3	3	7	4	78	по ведомости электроточек		л. 28, 29, 34, 35	950	74 100
17	Штробы в стенах под спуски кабеля к точкам — выполняются только после технического заключения о несущих стенах	м	48,10	6,60	17,00	4,46	13,80	20,00	16,80			6,60	6,60	16,80	6,57	163,33	Σ (H − h) по точкам на стенах: вертикальные спуски	после техзаключения	л. 15, 16, 28, 29	по КП	
18	Установка встраиваемого точечного светильника	шт	14	2	6	2	6	8	6			2	2	6	3	57	по плану освещения		л. 30, 31	750	42 750
19	Монтаж светильника: потолочного, подвесного, настенного	шт	3	1		1		2	1	1	1			1	1	12	по плану освещения		л. 30, 31	1 200	14 400
20	Монтаж LED-ленты в алюминиевый профиль	м	25,10		12,30		1,80	15,50	12,30					12,30		79,30	Σ длин лент по плану освещения		л. 30, 31	230	18 239
21	Установка блока питания LED в доступном месте (люк, шкаф)	шт	2		1		1	1	1					1		7	один на LED-группу		л. 30, 31	570	3 990
22	Установка автономного пожарного извещателя	шт	2	1	1		1	1	1			1	1	1		10	по плану розеток		л. 28, 29	по КП	

Допущения и предложения на листе

Основа листа: взаимное расположение помещений, контур дома 9600 × 8000 и раскладка этажей подобраны проектировщиком под габариты помещений брифа; обмер и проект АР — задание (К-1); высота потолка 2900 мм — по брифу, не замерена; перекрытие 330 мм и отметка 2-го этажа +3,230 приняты; проект КР — задание (К-2); наружные стены 400 мм, перегородки 120 мм приняты (в брифе толщин нет) (К-1); разрешённая мощность 15 кВт принята по типовым ТУ для частного дома (К-4).

Знак «**» — предложение проектировщика, заказчиком не утверждено (согласовать с заказчиком): записи в реестре нет: ЩС — щит слаботочный: место и состав.

См. лист открытых вопросов (лист 6, записи К-1, К-2, К-4).

Изм.	Кол.уч	Лист	№ док.	Подп.	Дата
Разраб.		Кырлан А.С.			19.10.26
Пров.					
ГИП					
Н. контр.					
Утв.					

ГД-2026-012-АИ

Дом 120 м²

Общая площадь 147,36* м² · * размеры приняты, не замерены (реестр — л. 6, К-1)

Дизайн-проект интерьера

Стадия	Лист	Листов
РП	124	130

Ведомость объёмов работ

М б/м

Кырлан Александр Сергеевич

Ведомость объёмов работ (продолжение)

Объёмы по помещениям от чертежа · площади в м², длины в м · формула, правило проёмов и источник в каждой строке

Ведомость объёмов работ по помещениям (продолжение)

Поз.	Наименование работ (материал, число слоёв)	Ед. изм.	Объём по помещениям (№ по экспликации)													Всего	Формула подсчёта	Правило проёмов	Источник	Цена за ед., ₽	Стоимость, ₽
			1	2	3	4	5	6	7	8	9	10	11	12	13						
23	Сборка щита: установка автоматов и АВДТ групп, вводного автомата	шт														18	группы + вводной автомат		л. 36, 37	230	4 140
24	Установка вводного УЗО	шт														1	по однолинейной схеме		л. 36, 37	380	380
25	Монтаж инсталляции, установка подвесного унитаза и кнопки смыва	шт				1									1	2	по плану выводов		л. 46, 47, 50	10 500	21 000
26	Короб инсталляции: каркас и обшивка ГКЛВ в 2 слоя, ревизионный доступ к смыву	шт				1									1	2	по плану выводов		л. 46, 47, 54–57	по КП	
27	Короб К1 над чистым полом: каркас и обшивка ГКЛВ под плитку (материалы — в спецификации ВК)	м.п.				3,05									5,87	8,92	Σ открытых участков выпусков К1 (профиль листа разводки ВК)		л. 46, 47, 50	по КП	
28	Установка ванны с сифоном	шт													1	1	по плану выводов		л. 46, 47, 50	6 000	6 000
29	Установка умывальника (мойки) с сифоном и смесителем	шт				1									1	2	по плану выводов		л. 46, 47, 50	3 000	6 000
30	Подключение стиральной (посудомоечной) машины к ВК	шт													1	1	по плану выводов		л. 46, 47	по КП	
31	Установка радиатора с узлом подключения и терморегулятором	шт	1	1	1			1	1			1		1		7	по плану отопления		л. 44, 45	по КП	
Итого по разделу 2 — 221 479 ₽ (позиций 22, из них по КП 11); в сводную смету — л. 129, 130																					
3. Чистовые работы																					
32	Облицовка стен керамогранитом 600×1200 на клею	м²				16,68									18,10	34,78	по раскладке: зона облицовки − место за коробом	за вычетом проёмов	л. 54–57	2 500	86 950
33	Облицовка короба инсталляции (ГКЛВ) керамогранитом: лицо, боковины, полка	м²				1,47									1,76	3,23	по раскладке: лицо, боковины, полка		л. 54–57	2 500	8 075
34	Облицовка фартука керамогранитом 1200×600	м²	2,00													2,00	по раскладке фартука		л. 54–57, 60, 61	2 400	4 800
35	Укладка керамогранита на пол, 600×1200, на клею	м²				4,24	12,54								5,40	22,18	S пом. + S в дверных проёмах	проёмы добавлены	л. 54–59	1 800	39 924
36	Затирка швов керамогранита	м²	2,00			22,32	12,20								25,17	61,69	Σ S облицовки и пола из плитки		л. 54–57	150	9 254
37	Грунтование стен, 2 слоя (под штукатурку и под отделку)	м²	56,72	34,65	34,81	21,65	43,20	43,93	36,92	22,06	23,61	34,65	19,31	31,55	23,78	426,84	P × H − проёмы	за вычетом проёмов	л. 60, 61	96	40 977
38	Шпаклёвка стен под окраску, 2 слоя (старт и финиш), уровень Q3	м²	54,72	34,65	34,81		43,20	43,93	36,92	22,06	23,61	34,65	19,31	31,55		379,41	P × H − проёмы − фартук	за вычетом проёмов	л. 60, 61	750	284 558
39	Грунтование и шпаклёвка оконных откосов, 2 слоя	м.п.	10,70	4,00	4,50			4,80	4,40			4,00		4,30		36,70	Σ (2h + b) по окнам	по окнам	л. 13, 14	300	11 010
40	Грунтование потолка, 2 слоя	м²	31,32	15,51	11,00	4,17	12,20	17,17	12,30	3,82	4,66	15,51	5,16	9,23	5,31	147,36	S пом.		л. 60, 61	96	14 147
41	Шпаклёвка потолка под окраску, 2 слоя, уровень Q3	м²	31,32	15,51	11,00	4,17	12,20	17,17	12,30	3,82	4,66	15,51	5,16	9,23	5,31	147,36	S пом.		л. 52, 53, 60, 61	950	139 992
42	Окраска потолка водно-дисперсионной краской, 2 слоя	м²	31,32	15,51	11,00	4,17	12,20	17,17	12,30	3,82	4,66	15,51	5,16	9,23	5,31	147,36	S пом.		л. 60, 61	360	53 050
43	Окраска стен водно-дисперсионной краской, 2 слоя	м²	63,42	46,86	38,74		50,34	48,31	40,77	23,32	25,29	46,86	26,45	35,26		445,62	P × H − фартук, проёмы не вычитаются	без вычета проёмов	л. 60, 61	300	133 686
44	Окраска оконных откосов, 2 слоя	м.п.	10,70	4,00	4,50			4,80	4,40			4,00		4,30		36,70	Σ (2h + b) по окнам	по окнам	л. 13, 14	120	4 404
45	Укладка инженерной доски на клей	м²	31,37	15,82	11,05			17,22	12,35	3,86	4,71	15,82	5,36	9,28		126,84	S пом. + S в дверных проёмах	проёмы добавлены	л. 58–61	1 200	152 208
46	Установка плинтуса МДФ h=80 мм	м.п.	21,66	11,06	12,56		13,96	15,86	13,26	7,44	7,92	11,06	5,72	11,36		131,86	P − ширина дверных проёмов		л. 60, 61	450	59 337
47	Окраска плинтуса в тоне G503, 2 слоя	м.п.	21,66	11,06	12,56		13,96	15,86	13,26	7,44	7,92	11,06	5,72	11,36		131,86	как плинтус		л. 60, 61	300	39 558
48	Монтаж дверей скрытого монтажа под покраску (поставщик дверей)	шт	1		1	1	1	1	1	1	1			1	1	10	по ведомости проёмов		л. 17, 18	5 250	52 500
49	Входная дверь, поставка с монтажом и откосами	шт														1	по ведомости проёмов		л. 17, 18	по КП	

Допущения и предложения на листе

Основа листа: взаимное расположение помещений, контур дома 9600 × 8000 и раскладка этажей подобраны проектировщиком под габариты помещений брифа; обмер и проект АР — задание (К-1); высота потолка 2900 мм — по брифу, не замерена; перекрытие 330 мм и отметка 2-го этажа +3,230 приняты; проект КР — задание (К-2); наружные стены 400 мм, перегородки 120 мм приняты (в брифе толщин нет) (К-1); разрешённая мощность 15 кВт принята по типовым ТУ для частного дома (К-4).

См. лист открытых вопросов (лист 6, записи К-1, К-2, К-4).

Изм.	Кол.уч	Лист	№ док.	Подп.	Дата
Разраб.		Кырлан А.С.			19.10.26
Пров.					
ГИП					
Н. контр.					
Утв.					

ГД-2026-012-АИ

Дом 120 м²

Общая площадь 147,36* м² · * размеры приняты, не замерены (реестр — л. 6, К-1)

Дизайн-проект интерьера

Стадия	Лист	Листов
РП	125	130

Ведомость объёмов работ (продолжение)

М б/м

Кырлан Александр Сергеевич

Ведомость объёмов работ (окончание)

Объёмы по помещениям от чертежа · площади в м², длины в м · формула, правило проёмов и источник в каждой строке

Ведомость объёмов работ по помещениям (продолжение)

Поз.	Наименование работ (материал, число слоёв)	Ед. изм.	Объём по помещениям (№ по экспликации)													Всего	Формула подсчёта	Правило проёмов	Источник	Цена за ед., ₽	Стоимость, ₽
			1	2	3	4	5	6	7	8	9	10	11	12	13						
Итого по разделу 3 — 1 134 430 ₽ (позиций 18, из них по КП 1); в сводную смету — л. 129, 130																					

Ведомость подсчёта площадей по помещениям

№	Помещение	S пола, м²	P, м	H, м	P × H, м²	Проёмы, м²	Стены нетто, м²	В дверных проёмах, м²	Плинтус, м	Откосы, м.п.
1	Гостиная-кухня	31,32	22,56	2,90	65,42	8,70	56,72	0,05	21,66	10,70
2	Холл с лестницей	15,51	16,16	2,90	46,86	12,21	34,65	0,31	11,06	4,00
3	Кабинет	11,00	13,36	2,90	38,74	3,93	34,81	0,05	12,56	4,50
4	Санузел гостевой	4,17	8,32	2,92	24,25	2,60	21,65	0,07	нет	нет
5	Прихожая	12,20	17,36	2,90	50,34	7,14	43,20	0,34	13,96	нет
6	Спальня родителей	17,17	16,66	2,90	48,31	4,38	43,93	0,05	15,86	4,80
7	Детская	12,30	14,06	2,90	40,77	3,85	36,92	0,05	13,26	4,40
8	Гардеробная	3,82	8,04	2,90	23,32	1,26	22,06	0,04	7,44	нет
9	Кладовая	4,66	8,72	2,90	25,29	1,68	23,61	0,05	7,92	нет
10	Холл второго этажа	15,51	16,16	2,90	46,86	12,21	34,65	0,31	11,06	4,00
11	Коридор второго этажа	5,16	9,12	2,90	26,45	7,14	19,31	0,20	5,72	нет
12	Детская вторая	9,23	12,16	2,90	35,26	3,71	31,55	0,05	11,36	4,30
13	Санузел второго этажа	5,31	9,24	2,92	26,93	3,15	23,78	0,09	нет	нет
	Итого	**147,36**			**498,83**	**71,97**	**426,86**	**1,65**	**131,86**	**36,70**

Реестр контрольных сумм

Показатель	По ВОР	По чертежу	Расхождение	Лист
Σ площадей помещений без летних, м² — общая площадь по экспликации	147,36	147,36	0,0 %	л. 13, 14
Стены под окраску, м² (шпаклёвка) ведомость отделки	379,41	379,43	0,0 %	л. 60, 61
Потолки под окраску, м² — ведомость отделки	147,36	147,36	0,0 %	л. 60, 61
Плинтус, м — ведомость отделки	131,86	131,86	0,0 %	л. 60, 61
Плитка к заказу, шт — ведомость плитки	154	154	0,0 %	л. 54
Гидроизоляция, м² — ведомость материалов плитки	17,77	17,78	0,0 %	л. 54
Точки ЭОМ, шт — планы ЭОМ (без щитов)	171	173	-1,2 %	л. 28–31

Примечания

1. Объёмы — от геометрии проекта (та же, что на планах и в ведомости отделки), не от общей площади: P — периметр чистого контура, H — от чистого пола до низа потолка, проёмы — по наружному обводу коробок.
2. Подсчёт по ГЭСН-2001-15 и ГЭСН-2001-11: штукатурка и шпаклёвка стен — за вычетом проёмов; окраска водными составами — без вычета проёмов (п. 2.24); откосы — отдельно, по ширине до 200 и более 200 мм; полы — с площадью в дверных проёмах.
3. Плитка — по раскладке (целые и с подрезкой); короб инсталляции и фартук — отдельными строками, двойного счёта облицовки нет. Материалы, запас и количество к заказу — в спецификации материалов.
4. Цены — ориентир по открытым прайсам Москвы (цены на 21.09.2026), не коммерческое предложение; «по КП» — расценки нет, строка в итог не входит.
5. Демонтаж — по плану демонтажа и общим указаниям: покрытия пола, отделка стен и потолков, дверные блоки — до основания; объёмы справочные, уточняются по факту на объекте (расценки в книге нет — «по КП»).
6. Штробы в стенах — только после технического заключения о несущих стенах (общие указания, план обмера и демонтажа): строка «Штробы в стенах» вертикальные спуски кабеля от потолочной трассы к точкам, объём не меньше фактического (горизонтальные трассы — по исполнительной схеме). Расценки штробления в прайсе нет — «по КП», в итог не входит; кабель в штробах стен прокладывается после неё.
7. Площадь облицовки стен — одно число с тремя названиями: зона облицовки по ведомости отделки 36,46 м² − место за коробом инсталляции 1,68 м² (плитку туда не кладут) = стены под плитку 34,78 м² (строка «Облицовка стен»); облицовка коробов 3,23 м² — отдельной строкой; стены и короба вместе — 38,01 м² (столько плитки по раскладке в спецификации). Источник — один (quantities.js), расхождение на листах ловит.
8. Слаботочные сети: кабель по лучам от ЩС** 93,80 м (U/UTP, RG-6, домофон — по видам), гофра 84,40 м, щит ЩС** с патч-панелью; розетки RJ45 и ТВ монтируются в строке «Электроточка». Длины те же, что в ведомости изделий электрика (одна модель — lowcurrent-engineer/bom.js); оборудование заказчика (точки доступа, камеры, коммутатор) в спецификацию не входит. 2 точ. — предложение листа слаботочки.
9. Коробы: стояков (нет) и К1 над чистым полом (8,93 м открытых участков; труба К1 вдоль стен 17,24 м в короб не зашивается — она за приборами, в раме инсталляции и в шахтах). В спецификации ВК короб К1 заказывается с запасом 10 % — 9,90 м. Материалы коробов стояков и инсталляции — в спецификации материалов, К1 — в спецификации ВК.

Допущения и предложения на листе

Основа листа: взаимное расположение помещений, контур дома 9600 × 8000 и раскладка этажей подобраны проектировщиком под габариты помещений брифа; обмер и проект АР — задание (К-1); высота потолка 2900 мм — по брифу, не замерена; перекрытие 330 мм и отметка 2-го этажа +3,230 приняты; проект КР — задание (К-2); наружные стены 400 мм, перегородки 120 мм приняты (в брифе толщин нет) (К-1); разрешённая мощность 15 кВт принята по типовым ТУ для частного дома (К-4).

Знак «**» — предложение проектировщика, заказчиком не утверждено (согласовать с заказчиком): записи в реестре нет: ЩС — щит слаботочный: место и состав.

См. лист открытых вопросов (лист 6, записи К-1, К-2, К-4).

Изм.	Кол.уч	Лист	№ док.	Подп.	Дата
Разраб.		Кырлан А.С.			19.10.26
Пров.					
ГИП					
Н. контр.					
Утв.					

ГД-2026-012-АИ

Дом 120 м²

Общая площадь 147,36* м² · * размеры приняты, не замерены (реестр — л. 6, К-1)

Дизайн-проект интерьера

Стадия	Лист	Листов
РП	126	130

Ведомость объёмов работ (окончание)

М б/м

Кырлан Александр Сергеевич

выпуск 19.10.2026 № 53e4f7ddae · стр. 133 из 160

Спецификация материалов

Отделочные материалы: чистое количество, запас, упаковка, к заказу · ГОСТ 21.110-2013

ПРЕДВАРИТЕЛЬНО · не для производства работ · открыто пунктов: 6 (реестр — л. 6)

Спецификация материалов (ГОСТ 21.110-2013, форма 1)

Поз.	Наименование и техническая характеристика	Тип, марка, артикул	Код продукции	Поставщик	Ед. изм.	Количество				Масса ед., кг	Примечание
						чистое	запас, %	упаковка	к заказу		
Покрытия полов и облицовка											
1	Инженерная доска (дуб натуральный, рабочий слой 4 мм, эмиссия E1, прямая укладка)	1167-4250			м²	126,83	7	по артикулу	135,80 м²		пом. 1, 2, 3, 6, 7, 8, 9, 10, 11, 12; до целой упаковки; л. 58–61
2	Клей для паркетной и инженерной доски (эластичный, по ТУ изготовителя доски)	по выбору подрядчика			м²	126,83		ведро по ТУ	по ТУ		расход кг/м² — по ТУ клея; л. 58, 59
3	Керамогранит 600×600 мм под травертин	аналог: керамогранит под травертин			шт	35	10	коробка	39 шт		9 целых + 26 с подрезкой; 9,48 м² по раскладке, к заказу 14,04 м²; пом. 4, 13; л. 54–57
4	Керамогранит 600×1200 мм под травертин	аналог: керамогранит под травертин			шт	78	10	коробка	88 шт		28 целых + 50 с подрезкой; 38,01 м² по раскладке, к заказу 63,36 м²; пом. 4, 13; л. 54–57
5	Керамогранит 600×1200 мм A8UZ	A8UZ			шт	18	10	коробка	20 шт		4 целых + 14 с подрезкой; 12,20 м² по раскладке, к заказу 14,40 м²; пом. 5; л. 54–57
6	Керамогранит 1200×600 мм под травертин, матовый	аналог: керамогранит под травертин, матовый			шт	5	10	коробка	7 шт		0 целых + 5 с подрезкой; 2,00 м² по раскладке, к заказу 5,04 м²; пом. 1; л. 54–57
Сухие смеси и гидроизоляция											
7	Клей плиточный цементный класса C2 TE S1 (ГОСТ Р 56387-2018)	Ceresit CM 17 или аналог			кг	447,45	10	мешок 25 кг	20 меш.	25	слой 5 мм, 1,50 кг/м² на 1 мм; л. 54
8	Затирка цементная класса CG2WA, цвет — по колерной карте	Mapei Ultracolor Plus 132 или аналог			кг	4,50	10	упак. 2 кг	3 упак.	2	расход (a+b)/ab × шов × t × 1,6 кг/м²; л. 54
9	Гидроизоляция обмазочная полимерная, 2 слоя, лента в углах, манжеты на выводах	по выбору подрядчика			м²	17,77	10	ведро по ТУ	по ТУ		пом. 4, 13; расход кг/м² — по ТУ; л. 54
10	Лента демпферная по периметру пола из плитки	по выбору подрядчика			м	25,12	10	рулон	28,00 м		л. 54
11	Смесь цементно-песчаная для стяжки М200 (50 мм, 33 мм)	по выбору подрядчика			м³	7,05	5	мешок по ТУ	по ТУ		S 144,31 м² × толщина; армирование и маяки — по ТУ; л. 58, 59
12	Смесь штукатурная гипсовая для машинного и ручного нанесения по маякам, слой до 10 мм	по выбору подрядчика			м²	403,23	10	мешок по ТУ	по ТУ		пом. 1, 2, 3, 4, 5, 6, 7, 8, 10, 11, 12, 13; расход кг/м² на 1 мм слоя по ТУ смеси, толщина — по замеру кривизны стен; л. 13, 14, 60, 61
Короба из ГКЛВ											
13	Лист ГКЛВ 12,5 мм, 2500 × 1200 мм, обшивка коробов в 2 слоя	по выбору подрядчика			м²	6,46	10	лист 3,00 м²	3,00 лист		инсталляция пом. 4: 1,47 м²; инсталляция пом. 13: 1,76 м²; площадь × 2 слоя; короб К1 над полом — в спецификации ВК; л. 46, 47, 54–57
14	Профиль стальной оцинкованный 27 × 28 мм: каркас коробов (стойки и направляющие)	по выбору подрядчика			м	15,60	10	хлыст 3 м	6 шт		стойки через 400 мм по свободному периметру + направляющие по полу и потолку; крепёж, лента, шпаклёвка швов — по узлу короба; л. 46, 47, 54–57
Слаботочные сети											
15	Кабель домофона — тип по системе поставщика	по выбору подрядчика			м	6,10		бухта по ТУ	7,00 м		по лучам от ЩС**, 1 точ., запас 10 % уже в длине; 2 точ. — предложение листа слаботочки (знак «*» на плане); л. 40, 41
16	Кабель коаксиальный RG-6 (75 Ом) к розеткам ТВ	по выбору подрядчика			м	16,70		бухта по ТУ	17,00 м		по лучам от ЩС**, 1 точ., запас 10 % уже в длине; 2 точ. — предложение листа слаботочки (знак «*» на плане); л. 40, 41
17	Кабель U/UTP кат. 6 (LAN, Wi-Fi и камеры по PoE)	по выбору подрядчика			м	71,00		бухта по ТУ	71,00 м		по лучам от ЩС**, 6 точ., запас 10 % уже в длине; 2 точ. — предложение листа слаботочки (знак «*» на плане); л. 40, 41
18	Гофротруба Ø20 для слаботочных линий, отдельно от силовых	по выбору подрядчика			м	84,40		бухта по ТУ	85,00 м		по длине лучей без участков в канале плинтуса (≈ 90 %); л. 40, 41
19	Розетка компьютерная RJ45, кат. 6, с рамкой и подрозетником	по выбору подрядчика			шт	4		шт	4 шт		LAN2, LAN3; серия механизмов — как у розеток и выключателей; л. 34, 35, 40, 41

Допущения и предложения на листе

Основа листа: взаимное расположение помещений, контур дома 9600 × 8000 и раскладка этажей подобраны проектировщиком под габариты помещений брифа; обмер и проект АР — задание (К-1); высота потолка 2900 мм — по брифу, не замерена; перекрытие 330 мм и отметка 2-го этажа +3,230 приняты; проект КР — задание (К-2); наружные стены 400 мм, перегородки 120 мм приняты (в брифе толщин нет) (К-1); разрешённая мощность 15 кВт принята по типовым ТУ для частного дома (К-4).

Знак «**» — предложение проектировщика, заказчиком не утверждено (согласовать с заказчиком): записи в реестре нет: ЩС — щит слаботочный: место и состав; плинтус пом. 1–3, 5, 6, 8, 10, 11, фартук пом. 1 — артикул изделия не выбран: позиция описана характеристиками («аналог по характеристикам»), артикул выбирается при закупке.

См. лист открытых вопросов (лист 6, записи К-1, К-2, К-4).

Изм.	Кол.уч	Лист	№ док.	Подп.	Дата
Разраб.		Кырлан А.С.			19.10.26
Пров.					
ГИП					
Н. контр.					
Утв.					

ГД-2026-012-АИ

Дом 120 м²

Общая площадь 147,36* м² · * размеры приняты, не замерены (реестр — л. 6, К-1)

Дизайн-проект интерьера

Стадия	Лист	Листов
РП	127	130

Спецификация материалов

М б/м

Кырлан Александр Сергеевич

Спецификация материалов (окончание)

Отделочные материалы: чистое количество, запас, упаковка, к заказу · ГОСТ 21.110-2013

Спецификация материалов (ГОСТ 21.110-2013, форма 1) (продолжение)

Поз.	Наименование и техническая характеристика	Тип, марка, артикул	Код продукции	Поставщик	Ед. изм.	Количество				Масса ед., кг	Примечание
						чистое	запас, %	упаковка	к заказу		
20	Розетка телевизионная (коаксиальная) с рамкой и подрозетником	по выбору подрядчика			шт	1		шт	1 шт		ТВ1; серия механизмов — как у розеток и выключателей; л. 34, 35, 40, 41
21	Трубка или монитор домофона (поставка домофонной организации)	по выбору подрядчика			шт	1		шт	1 шт		ДФ1; серия механизмов — как у розеток и выключателей; л. 34, 35, 40, 41
22	Щит слаботочный ЩС**: корпус, DIN-рейка, розетки 220 В	по выбору подрядчика			шт	1		шт	1 шт		ЩС**; серия механизмов — как у розеток и выключателей; л. 34, 35, 40, 41
23	Патч-панель, портов не менее 6	по выбору подрядчика			шт	1		шт	1 шт		серия механизмов — как у розеток и выключателей; л. 34, 35, 40, 41
Лакокрасочные материалы											
24	Краска интерьерная акриловая, матовая, класс истирания 1	Farrow & Ball Modern Emulsion S 3050-R80B «Эгейский синий»			л	2,78	10	банка 2,5 л	2 банк		11,58 м² × 2 сл. × 0,12 л/м²; пом. 1; л. 60, 61
25	Краска интерьерная акриловая, матовая, класс истирания 1	Farrow & Ball Modern Emulsion G503 «Calla»			л	68,38	10	банка 2,5 л	31 банк		284,93 м² × 2 сл. × 0,12 л/м²; пом. 1, 2, 3, 5, 6, 7, 10, 11, 12; л. 60, 61
26	Краска интерьерная акриловая, глубокоматовая, класс истирания 2	Tikkurila Anti-Reflex 2 No. 222 «Loft White»			л	31,97	10	банка 2,7 л	14 банк		133,22 м² × 2 сл. × 0,12 л/м²; пом. 1 (пот.), 2 (пот.), 3 (пот.), 5 (пот.), 6 (пот.), 7 (пот.), 8 (пот.), 10 (пот.), 11 (пот.), 12 (пот.); л. 60, 61
27	Краска интерьерная акриловая, матовая, класс истирания 1	Farrow & Ball Modern Emulsion S 5020-G90Y «Олива»			л	2,60	10	банка 2,5 л	2 банк		10,85 м² × 2 сл. × 0,12 л/м²; пом. 3; л. 60, 61
28	Краска интерьерная акриловая, матовая, класс истирания 1	Tikkurila Luja 7 No. 222 «Loft White»			л	2,28	10	банка 2,7 л	1 банк		9,48 м² × 2 сл. × 0,12 л/м²; пом. 4 (пот.), 13 (пот.); л. 60, 61
29	Краска интерьерная акриловая, матовая, класс истирания 1	Farrow & Ball Modern Emulsion No. 89 «Lulworth Blue — светлая морская лазурь»			л	1,96	10	банка 2,5 л	1 банк		8,15 м² × 2 сл. × 0,12 л/м²; пом. 6; л. 60, 61
30	Краска интерьерная акриловая, матовая, класс истирания 1	Farrow & Ball Modern Emulsion No. 66 «India Yellow — охра / горчица итальянских фасадов»			л	2,60	10	банка 2,5 л	2 банк		10,85 м² × 2 сл. × 0,12 л/м²; пом. 7; л. 60, 61
31	Краска интерьерная акриловая, матовая, класс истирания 1	Tikkurila Harmony No. 222 «Loft White»			л	5,29	10	банка 2,7 л	3 банк		22,06 м² × 2 сл. × 0,12 л/м²; пом. 8; л. 60, 61
32	Краска интерьерная акриловая, матовая, класс истирания 2	Tikkurila S 0502-Y			л	5,67	10	банка 2,7 л	3 банк		23,61 м² × 2 сл. × 0,12 л/м²; пом. 9; л. 60, 61
33	Краска интерьерная водно-дисперсионная, глубокоматовая, класс истирания 2	Tikkurila S 0300-N			л	1,12	10	банка 2,7 л	1 банк		4,66 м² × 2 сл. × 0,12 л/м²; пом. 9 (пот.); л. 60, 61
34	Краска интерьерная акриловая, матовая, класс истирания 1	Farrow & Ball Modern Emulsion H440 «H440 Wave — бирюзово-голубая вода»			л	1,78	10	банка 2,5 л	1 банк		7,43 м² × 2 сл. × 0,12 л/м²; пом. 12; л. 60, 61
35	Шпаклёвка финишная полимерная под окраску (стены и потолки, Q3)	по выбору подрядчика			м²	526,77	10	ведро по ТУ	по ТУ		расход кг/м² на слой — по ТУ; л. 60, 61
36	Грунтовка акриловая глубокого проникновения, 2 слоя	по выбору подрядчика			м²	574,20	10	канистра по ТУ	по ТУ		расход л/м² — по ТУ; л. 60, 61
Погонажные изделия и потолки											
37	Плинтус напольный МДФ под покраску, h=80 мм, крепление к стене	аналог: плинтус МДФ под покраску 80×16			м.п.	99,32	10	хлыст 2,4 м	46 шт		пом. 1, 2, 3, 5, 6, 8, 10, 11; длина хлыста — по артикулу; л. 60, 61
38	Плинтус напольный МДФ под покраску, h=69 мм, крепление к стене	SX165			м.п.	32,54	10	хлыст 2,4 м	15 шт		пом. 7, 9, 12; длина хлыста — по артикулу; л. 60, 61

Примечания

1. Чистое количество — из ведомости объёмов работ и раскладки плитки; запас — отдельной графой (доска — по ведомости отделки, плитка, краска и плинтус — 10 %); «к заказу» — с запасом и кратно упаковке.
2. Плитка — штуками по раскладке, запас на каждую поверхность. Калибр (рабочий размер) и тон — одной партией на помещение, калибр указать при заказе и сверить с раскладкой до укладки.
3. Краска — 0,12 л/м² на слой (середина вилки 0,10–0,15 л/м²) по фактической площади окраски из ведомости отделки; колеровка одной партией.
4. «По ТУ» — расход задаёт производитель выбранного продукта; количество к заказу — после выбора марки.
5. Поз. 3, 4, 6, 37 заданы характеристиками («аналог:»): марку, артикул и поставщика согласовать с заказчиком до закупки, без артикула не заказывать.
6. Штукатурная смесь — на ту же площадь, что строка ВОР «Штукатурка стен» (403,23 м²): площадь одна, расход смеси задаёт производитель.
7. Коробы инсталляции и стояков: ГКЛВ в 2 слоя и профиль 27 × 28 мм считаются по свободным граням коробов (источник — раскладка плиточника и шахты в данных); короб К1 над полом — в спецификации ВК.
8. Потолки ГКЛ: в этой спецификации — площадь системы П113; число листов, профилей и подвесов — по шагам каркаса на листе потолков (подвесы через 1000, несущие через 500, основные через 1200 мм), схема каркаса не выпущена. Сантехника, светильники и мебель — по своим спецификациям.

Допущения и предложения на листе

Основа листа: взаимное расположение помещений, контур дома 9600 × 8000 и раскладка этажей подобраны проектировщиком под габариты помещений брифа; обмер и проект АР — задание (К-1); высота потолка 2900 мм — по брифу, не замерена; перекрытие 330 мм и отметка 2-го этажа +3,230 приняты; проект КР — задание (К-2); наружные стены 400 мм, перегородки 120 мм приняты (в брифе толщин нет) (К-1); разрешённая мощность 15 кВт принята по типовым ТУ для частного дома (К-4).

Знак «**» — предложение проектировщика, заказчиком не утверждено (согласовать с заказчиком): записи в реестре нет: ЩС — щит слаботочный: место и состав; плинтус пом. 1–3, 5, 6, 8, 10, 11, фартук пом. 1 — артикул изделия не выбран: позиция описана характеристиками («аналог по характеристикам»), артикул выбирается при закупке.

См. лист открытых вопросов (лист 6, записи К-1, К-2, К-4).

Изм.	Кол.уч	Лист	№ док.	Подп.	Дата
Разраб.		Кырлан А.С.			19.10.26
Пров.					
ГИП					
Н. контр.					
Утв.					

ГД-2026-012-АИ

Дом 120 м²

Общая площадь 147,36* м² · * размеры приняты, не замерены (реестр — л. 6, К-1)

Дизайн-проект интерьера	Стадия	Лист	Листов
	РП	128	130

Спецификация материалов (окончание)

М б/м

Кырлан Александр Сергеевич

выпуск 19.10.2026 № 53e4f7ddae · стр. 135 из 160

Смета ориентировочная

ПРЕДВАРИТЕЛЬНО · не для производства работ · открыто пунктов: 6 (реестр — л. 6)

Работы, материалы, оборудование, услуги и резерв · цены — ориентир по открытым прайсам, не коммерческое предложение

Сводная смета (цены на 21.09.2026, Москва)

№	Наименование работ, материалов, услуг	Ед. изм.	Кол-во	Цена за ед., ₽	Стоимость, ₽			Чей подряд	Срок поставки, дн.	Основание	Источник цены
					план	факт	разница				
Работы — по ведомости объёмов работ											
1	Демонтаж и черновые работы (без 5 поз. по КП)	раздел	1		304 732			бригада		ВОР, поз. 1–9; л. 124–126	по ВОР
2	Инженерные системы (без 11 поз. по КП)	раздел	1		221 479			бригада		ВОР, поз. 10–31; л. 124–126	по ВОР
3	Чистовые работы (без 1 поз. по КП)	раздел	1		1 134 430			бригада, поставщик		ВОР, поз. 32–49; л. 124–126	по ВОР
Материалы — по спецификации материалов											
4	Инженерная доска	м²	135,80	4 513	612 865			поставщик		спецификация, поз. 1	Ц7
5	Керамогранит 600×600 мм	м²	14,04	1 800	25 272			поставщик		спецификация, поз. 3	Ц6
6	Керамогранит 600×1200, 1200×600 мм	м²	82,80	3 500	289 800			поставщик		спецификация, поз. 4, 5, 6	Ц6
7	Клей плиточный цементный класса C2 TE S1	меш.	20	1 800	36 000			поставщик		спецификация, поз. 7	Ц7
8	Затирка цементная класса CG2WA	упак.	3	1 000	3 000			поставщик		спецификация, поз. 8	Ц7
9	Краска Farrow & Ball Modern Emulsion, банка 2,5 л	банк	39	5 800	226 200			поставщик		спецификация, поз. 24, 25, 27, 29, 30, 34	Ц7
10	Краска Tikkurila (Anti-Reflex 2, Luja 7, Harmony), банка 2,7 л	банк	22	3 510	77 220			поставщик		спецификация, поз. 26, 28, 31, 32, 33	Ц6
11	Плинтус напольный МДФ под покраску	шт	61	368	22 448			поставщик		спецификация, поз. 37, 38	Ц7
12	Прочие материалы с расходом по ТУ (клей для доски, гидроизоляция, демпферная лента, смесь для стяжки, смесь штукатурная гипсовая для машинного и ручного нанесения по маякам, лист гклв 12, профиль стальной оцинкованный 27 × 28 мм: каркас коробов (стойки и направляющие), кабель слаботочки, гофра слаботочки, изделия слаботочки, шпаклёвка, грунтовка)	компл	1	по КП				поставщик		спецификация, поз. 2, 9, 10, 11, 12, 13, 14, 15, 16, 17, 18, 19, 20, 21, 22, 23, 35, 36	
Оборудование и мебель — поставка по спецификациям											
13	Кухонный гарнитур по проекту кухни, изготовление и монтаж (4–8 нед.)	компл	1	по КП				поставщик	уточн.; ориентир 4–8 нед. от замера	л. 85–88	

Допущения и предложения на листе

Основа листа: взаимное расположение помещений, контур дома 9600 × 8000 и раскладка этажей подобраны проектировщиком под габариты помещений брифа; обмер и проект АР — задание (К-1); высота потолка 2900 мм — по брифу, не замерена; перекрытие 330 мм и отметка 2-го этажа +3,230 приняты; проект КР — задание (К-2); наружные стены 400 мм, перегородки 120 мм приняты (в брифе толщин нет) (К-1); разрешённая мощность 15 кВт принята по типовым ТУ для частного дома (К-4).

См. лист открытых вопросов (лист 6, записи К-1, К-2, К-4).

Изм.	Кол.уч	Лист	№ док.	Подп.	Дата
Разраб.		Кырлан А.С.			19.10.26
Пров.					
ГИП					
Н. контр.					
Утв.					

ГД-2026-012-АИ

Дом 120 м²

Общая площадь 147,36* м² · * размеры приняты, не замерены (реестр — л. 6, К-1)

Дизайн-проект интерьера

Стадия	Лист	Листов
РП	129	130

Смета ориентировочная

М б/м

Кырлан Александр Сергеевич

Смета ориентировочная (окончание)

Работы, материалы, оборудование, услуги и резерв · цены — ориентир по открытым прайсам, не коммерческое предложение

Сводная смета (цены на 21.09.2026, Москва) (продолжение)

№	Наименование работ, материалов, услуг	Ед. изм.	Кол-во	Цена за ед., ₽	Стоимость, ₽			Чей подряд	Срок поставки, дн.	Основание	Источник цены
					план	факт	разница				
14	Двери скрытого монтажа с коробом под покраску, поставка	шт	10	по КП				поставщик	уточн.; ориентир ≈ 30 дн.	л. 17, 18	
15	Оборудование заказчика слаботочных сетей: точка доступа wi-fi — 2 шт; коммутатор — 1 шт	компл	1	по КП				заказчик		л. 34, 35	
16	Сантехника, светильники, мебель и предметы интерьера	компл	1	по КП				поставщик		л. 50; л. 51; л. 91; л. 24–27	
Прочие работы и услуги											
17	Вынос и вывоз строительного мусора	м³		по факту				бригада		после демонтажа	
18	Подъём материалов на этаж (лифтом или вручную — по договору)	т		по факту				бригада		по массе поставки	
19	Доставка чистовых материалов, 10 % от поставки			10 %	129 281			поставщик		от суммы материалов	
20	Уборка после ремонта	м²	147,36	по факту				бригада		S квартиры	
	Итого работы				**1 660 641**						
	Итого материалы				**1 292 805**						
	Итого прочие услуги				**129 281**						
	Резерв на непредвиденные работы и материалы, 15 %				**462 409**						
	ВСЕГО ориентировочно (без оборудования и позиций по КП)				**3 545 136**						

Примечания

1. Смета ориентировочная, не коммерческое предложение: объёмы — из ведомости объёмов работ и спецификации материалов, цены — нижняя граница открытых прайсов Москвы (цены на 21.09.2026); перед договором цены подтвердить у подрядчика и поставщиков.
2. Источники цен: Ц1 — Домашний мастерок: прайс на отделочные работы, 2026; Ц2 — Домашний мастерок: прайс на плиточные работы, 2026; Ц3 Домашний мастерок: прайс на электромонтажные работы, 2026; Ц4 — Профи ремонтник: штукатурно-малярные работы; Ц5 — Profi.ru: укладка керамогранита на стены, Москва 2026; Ц6 — knowledge/spec-materials.md, разд. 1 и 3: ориентир по сегментам; Ц7 — Розница Москвы, 09.2026: Лемана ПРО, KGSnab, официальный дилер Farrow & Ball.
3. В итог не вошли позиции «по КП» и «по факту»: оборудование и мебель, двери, материалы с расходом по ТУ, вывоз мусора, подъём и уборка.
4. Доставка — 10 % от материалов, резерв — 15 % (частный ремонт 10–20 %) отдельными строками, в количествах не спрятаны. Графы «факт» и «разница» заполняются по актам.

Допущения и предложения на листе

Основа листа: взаимное расположение помещений, контур дома 9600 × 8000 и раскладка этажей подобраны проектировщиком под габариты помещений брифа; обмер и проект АР — задание (К-1); высота потолка 2900 мм — по брифу, не замерена; перекрытие 330 мм и отметка 2-го этажа +3,230 приняты; проект КР — задание (К-2); наружные стены 400 мм, перегородки 120 мм приняты (в брифе толщин нет) (К-1); разрешённая мощность 15 кВт принята по типовым ТУ для частного дома (К-4).
См. лист открытых вопросов (лист 6, записи К-1, К-2, К-4).

Изм.	Кол.уч	Лист	№ док.	Подп.	Дата
Разраб.		Кырлан А.С.			19.10.26
Пров.					
ГИП					
Н. контр.					
Утв.					

ГД-2026-012-АИ

Дом 120 м²

Общая площадь 147,36* м² · * размеры приняты, не замерены (реестр — л. 6, К-1)

Дизайн-проект интерьера	Стадия	Лист	Листов
	РП	130	130

Смета ориентировочная (окончание)

М б/м

Кырлан Александр Сергеевич

06

Визуализации

Кырлан Александр Сергеевич

выпуск 19.10.2026 № 53e4f7ddae · стр. 138 из 160

3d-top-et1

Дом 120 м² · визуализация 1 из 22

выпуск 19.10.2026 № 53e4f7ddae · стр. 139 из 160

3d-top-et2

Дом 120 м² · визуализация 2 из 22

выпуск 19.10.2026 № 53e4f7ddae · стр. 140 из 160

выпуск 19.10.2026 № 53e4f7ddae · стр. 141 из 160

room-bath-wide

room-bedroom-wC

Дом 120 м² · визуализация 4 из 22

выпуск 19.10.2026 № 53e4f7ddae · стр. 142 из 160

room-bedroom-wD

Дом 120 м² · визуализация 5 из 22

room-corridor1-wB

Дом 120 м² · визуализация 6 из 22

выпуск 19.10.2026 № 53e4f7ddae · стр. 145 из 160

room-corridor2-wide

выпуск 19.10.2026 № 53e4f7ddae · стр. 146 из 160

room-corridor3-wide

room-hall-wA

Дом 120 м² · визуализация 9 из 22

выпуск 19.10.2026 № 53e4f7ddae · стр. 147 из 160

room-hall-wB

Дом 120 м² · визуализация 10 из 22

выпуск 19.10.2026 № 53e4f7ddae · стр. 148 из 160

room-kids1-wA

Дом 120 м² · визуализация 11 из 22

выпуск 19.10.2026 № 53e4f7ddae · стр. 149 из 160

выпуск 19.10.2026 № 53e4f7ddae · стр. 150 из 160

room-kids1-wC

room-kids2-wA

Дом 120 м² · визуализация 13 из 22

room-kids2-wD

Дом 120 м² · визуализация 14 из 22

room-living-wA

Дом 120 м² · визуализация 15 из 22

выпуск 19.10.2026 № 53e4f7ddae · стр. 153 из 160

room-living-wB

Дом 120 м² · визуализация 16 из 22

выпуск 19.10.2026 № 53e4f7ddae · стр. 155 из 160

room-living-wC

room-storage-wide

Дом 120 м² · визуализация 18 из 22

выпуск 19.10.2026 № 53e4f7ddae · стр. 156 из 160

room-study-wA

Дом 120 м² · визуализация 19 из 22

выпуск 19.10.2026 № 53e4f7ddae · стр. 158 из 160

room-study-wC

room-wardrobe-wide

Дом 120 м² · визуализация 21 из 22

выпуск 19.10.2026 № 53e4f7ddae · стр. 159 из 160

room-wc-wide

Дом 120 м² · визуализация 22 из 22

выпуск 19.10.2026 № 53e47ddae · стр. 160 из 160