ДИЗАЙН-ПРОЕКТ ИНТЕРЬЕРА

Дом 120 м²

Средиземноморский

147,36 м²

солнце и воздух · морская свежесть · неторопливость · тёплая простота · жизнь на террасе

Средиземноморский 60 % + скандинавский (scandinavian.json) 40 %: дом у соснового бора, светлый и солнечный. Стены — кремовый белый Calla G503 и известковый Wimborne White No. 239, потолки — Loft White No. 222; второй план светлый песок S 1010-Y20R, морская лазурь Lulworth Blue No. 89, серо-оливковая листва Treron No. 292; акценты эгейский синий S 3050-R80B, охра India Yellow No. 66, олива S 5020-G90Y. По брифу: дерево — дуб табак (мебель, лестница), фурнитура и светильники — латунь, рамы и металл — тёплый графит; свет тёплый 2700–3000 K, фасады матовые.

ПАЛИТРА 60 / 30 / 10

G503	F&B No. 239	Little Greene No. 222	NCS S 1010-Y20R	F&B No. 89
60 %	60 %	60 %	30 %	30 %

АВТОР ПРОЕКТА

Кырлан Александр Сергеевич

Октябрь 2026



Визуализация 1 · Вид сверху (3D): планировка с мебелью, текстилем и декором

ОБЪЕКТ	ОБЩАЯ ПЛОЩАДЬ	ПОМЕЩЕНИЙ
Дом 120 м²	147,36 м²	13, из них жилых 5
СТИЛЬ	**СТАДИЯ**	**ШИФР**
Средиземноморский	Рабочий проект	ГД-2026-012-АИ

					Проект: Дом 120 м²
	Лист	№ док.	Подпись	Дата	Титульный лист
Дизайнер	Кырлан А.С.			19.10.26	Стадия: П; Лист: 1; Листов: 128

выпуск 19.10.2026 № 66b2a77b4d · стр. 1 из 128

Список листов


Лист	Наименование
1	Титульный лист
2	Список листов
3	План планировки от заказчика · 1-й этаж
4	План планировки от заказчика · 2-й этаж
5	План монтажный · 1-й этаж
6	План монтажный · 2-й этаж
7	Кухня (пом. 1). Монтажная схема
8	Кухня (пом. 1). Монтажная схема
9	Шкафы. Монтажная схема. Лист 1 из 2
10	Шкафы. Монтажная схема. Лист 2 из 2
11	Карта покрытий стен · 1-й этаж
12	Карта покрытий стен · 2-й этаж
13	Колерная карта · 1-й этаж
14	Колерная карта · 2-й этаж
15	План размещения мебели и оборудования · 1-й этаж
16	План размещения мебели и оборудования · 2-й этаж
17	Спецификация мебели и оборудования
18	Спецификация мебели и оборудования (продолжение)
19	Спецификация мебели и оборудования (продолжение)
20	Ведомости изделий, техники и фурнитуры
21	План выводов сантехники · 1-й этаж
22	План выводов сантехники · 2-й этаж
23	Схема разводки водопровода и канализации · 1-й этаж
24	Схема разводки водопровода и канализации · 2-й этаж
25	Спецификация сантехнического оборудования
26	Раскладка плитки. Санузел гостевой. Развёртки стен
27	Раскладка плитки. Санузел второго этажа. Развёртки стен
28	План размещения дверей · 1-й этаж
29	План размещения дверей · 2-й этаж
30	Лестница Л-1
31	План потолков · 1-й этаж
32	План потолков · 2-й этаж
33	План розеток и электровыводов · 1-й этаж
34	План розеток и электровыводов · 2-й этаж
35	План слаботочных сетей · 1-й этаж
36	План слаботочных сетей · 2-й этаж
37	План освещения · 1-й этаж
38	План освещения · 2-й этаж
39	Спецификация светильников и сценарии освещения
40	Управление светильниками · 1-й этаж
41	Управление светильниками · 2-й этаж
42	План вентиляции · 1-й этаж
43	План вентиляции · 2-й этаж
44	План отопления · 1-й этаж
45	План отопления · 2-й этаж
46	План покрытий пола · 1-й этаж
47	План покрытий пола · 2-й этаж
48	Раскладка плитки. Планы полов
49	Раскладка плитки. Прихожая. Фартук кухни
50	Визуализация. Вид сверху
51	Визуализация. Вид сверху
52	Визуализация: Гостиная-кухня
53	Визуализация: Гостиная-кухня
54	Визуализация: Гостиная-кухня
55	Развёртка стены А. Гостиная-кухня (пом. 1), кухонный фронт
56	Развёртка стены Б. Гостиная-кухня (пом. 1), кухонный фронт
57	Развёртка стены В. Гостиная-кухня (пом. 1)
58	Развёртка стены Г. Гостиная-кухня (пом. 1)
59	Визуализация: Холл с лестницей
60	Развёртка стены А. Холл с лестницей (пом. 2)
61	Развёртка стены В. Холл с лестницей (пом. 2)
62	Развёртка стены Г. Холл с лестницей (пом. 2)
63	Визуализация кабинета
64	Визуализация кабинета
65	Развёртка стены А. Кабинет (пом. 3)
66	Развёртка стены Б. Кабинет (пом. 3)
67	Развёртка стены В. Кабинет (пом. 3)
68	Развёртка стены Г. Кабинет (пом. 3)
69	Визуализация: Санузел гостевой
70	Развёртка стены А. Санузел гостевой (пом. 4)
71	Развёртка стены Б. Санузел гостевой (пом. 4)
72	Развёртки стен В, Г. Санузел гостевой (пом. 4)
73	Визуализация прихожей
74	Визуализация прихожей
75	Развёртка стены А1. Прихожая (пом. 5)
76	Развёртка стены А2. Прихожая (пом. 5)
77	Развёртка стены Б. Прихожая (пом. 5)
78	Развёртка стены В. Прихожая (пом. 5)
79	Развёртки стен Г1, Г2. Прихожая (пом. 5)
80	Визуализация: Спальня родителей
81	Визуализация: Спальня родителей
82	Развёртка стены А. Спальня родителей (пом. 6)
83	Развёртка стены Б. Спальня родителей (пом. 6)
84	Развёртка стены В. Спальня родителей (пом. 6)
85	Развёртка стены Г. Спальня родителей (пом. 6)
86	Визуализация детской
87	Визуализация детской
88	Развёртка стены А. Детская (пом. 7)
89	Развёртка стены Б. Детская (пом. 7)
90	Развёртка стены В. Детская (пом. 7)
91	Развёртка стены Г. Детская (пом. 7)
92	Визуализация гардеробной
93	Развёртки стен А, Б. Гардеробная (пом. 8)
94	Развёртки стен В, Г. Гардеробная (пом. 8)
95	Визуализация кладовой
96	Развёртки стен Б, В. Кладовая (пом. 9)
97	Развёртка стены Г. Кладовая (пом. 9)
98	Визуализация: Холл второго этажа
99	Развёртка стены А. Холл второго этажа (пом. 10)
100	Развёртка стены В. Холл второго этажа (пом. 10)
101	Развёртка стены Г. Холл второго этажа (пом. 10)
102	Визуализация: Коридор второго этажа
103	Развёртки стен А, В. Коридор второго этажа (пом. 11)
104	Развёртка стены Г. Коридор второго этажа (пом. 11)
105	Визуализация: Детская вторая
106	Визуализация: Детская вторая
107	Развёртка стены А. Детская вторая (пом. 12)
108	Развёртка стены Б. Детская вторая (пом. 12)
109	Развёртка стены В. Детская вторая (пом. 12)
110	Развёртка стены Г. Детская вторая (пом. 12)
111	Визуализация: Санузел второго этажа
112	Развёртки стен А, Б. Санузел второго этажа (пом. 13)
113	Развёртка стены В. Санузел второго этажа (пом. 13)
114	Развёртка стены Г. Санузел второго этажа (пом. 13)
Д_1	Шкаф-купе М_25
Д_2	Шкаф распашной М_30

	Лист	№ док.	Подпись	Дата
Дизайнер	Кирлан А.О.			19.10.26

Проект: Дом 120 м²

Список листов	Стадия	Лист	Листов
	П	2	128

выпуск 19.10.2026 № 66b2a77b4d · стр. 2 из 128

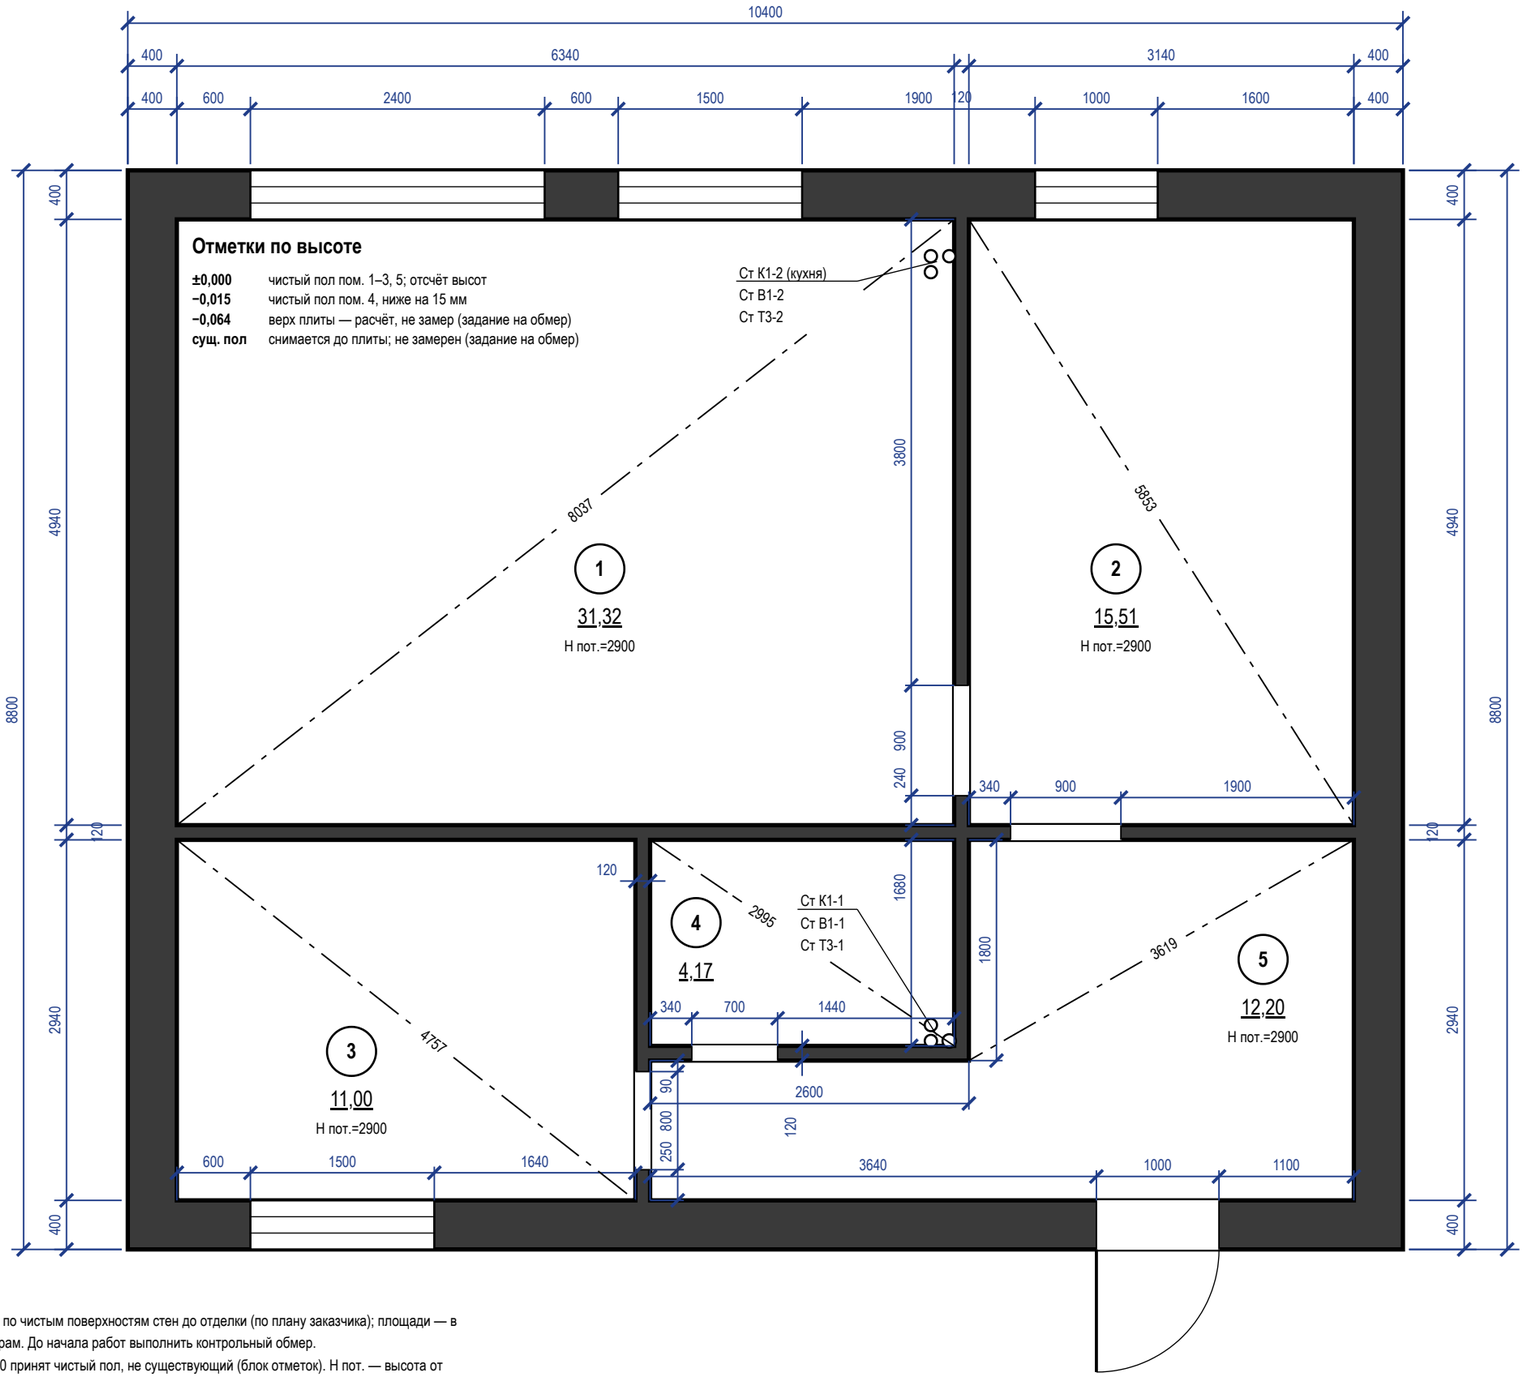

Экспликация помещений

№	Наименование	Площадь, м²
1	Гостиная-кухня	31,32
2	Холл с лестницей	15,51
3	Кабинет	11,00
4	Санузел гостевой	4,17
5	Прихожая	12,20
	Итого (общая площадь)	**147,36**

Условные обозначения

- существующие стены (сечение)
- окно (рама, остекление)
- проём существующий, без заполнения (откосы)
- стояк: К1 — канализация, В1 — ХВС, Т3 — ГВС
- диагональ помещения — контроль прямоугольности
- (1) номер помещения, площадь м²

Примечания

1. Размеры — в мм по чистым поверхностям стен до отделки (по плану заказчика); площади — в м² по тем же размерам. До начала работ выполнить контрольный обмер.
2. За отметку ±0,000 принят чистый пол, не существующий (блок отметок). Н пот. — высота от чистого пола до плиты перекрытия.
3. Толщины стен: наружные 400 мм, перегородки 120 мм; отличающиеся толщины и уступы размерами на плане.
4. Несущие стены не определены: до технического заключения все стены считать несущими; проёмы и штробы в них не выполнять.
5. Дверные проёмы показаны без заполнения; высота дверных проёмов 2100 мм; низ окон (подоконник) 500, 900 мм от чистого пола, высота окон 1900, 1500 мм.
6. Диагонали — контрольные размеры; расхождение более 5 мм подписать на плане как перекос.
7. Размеры проверить на месте до начала работ; расхождение контрольных промеров ≤ 2 %.


	Лист	№ док.	Подпись	Дата
Дизайнер	Кырлан А.С.			19.10.26

Проект: Дом 120 м²

План планировки от заказчика · 1-й этаж

Стадия	Лист	Листов
П	3	128

выпуск 19.10.2026 № 66b2a77b4d · стр. 3 из 128

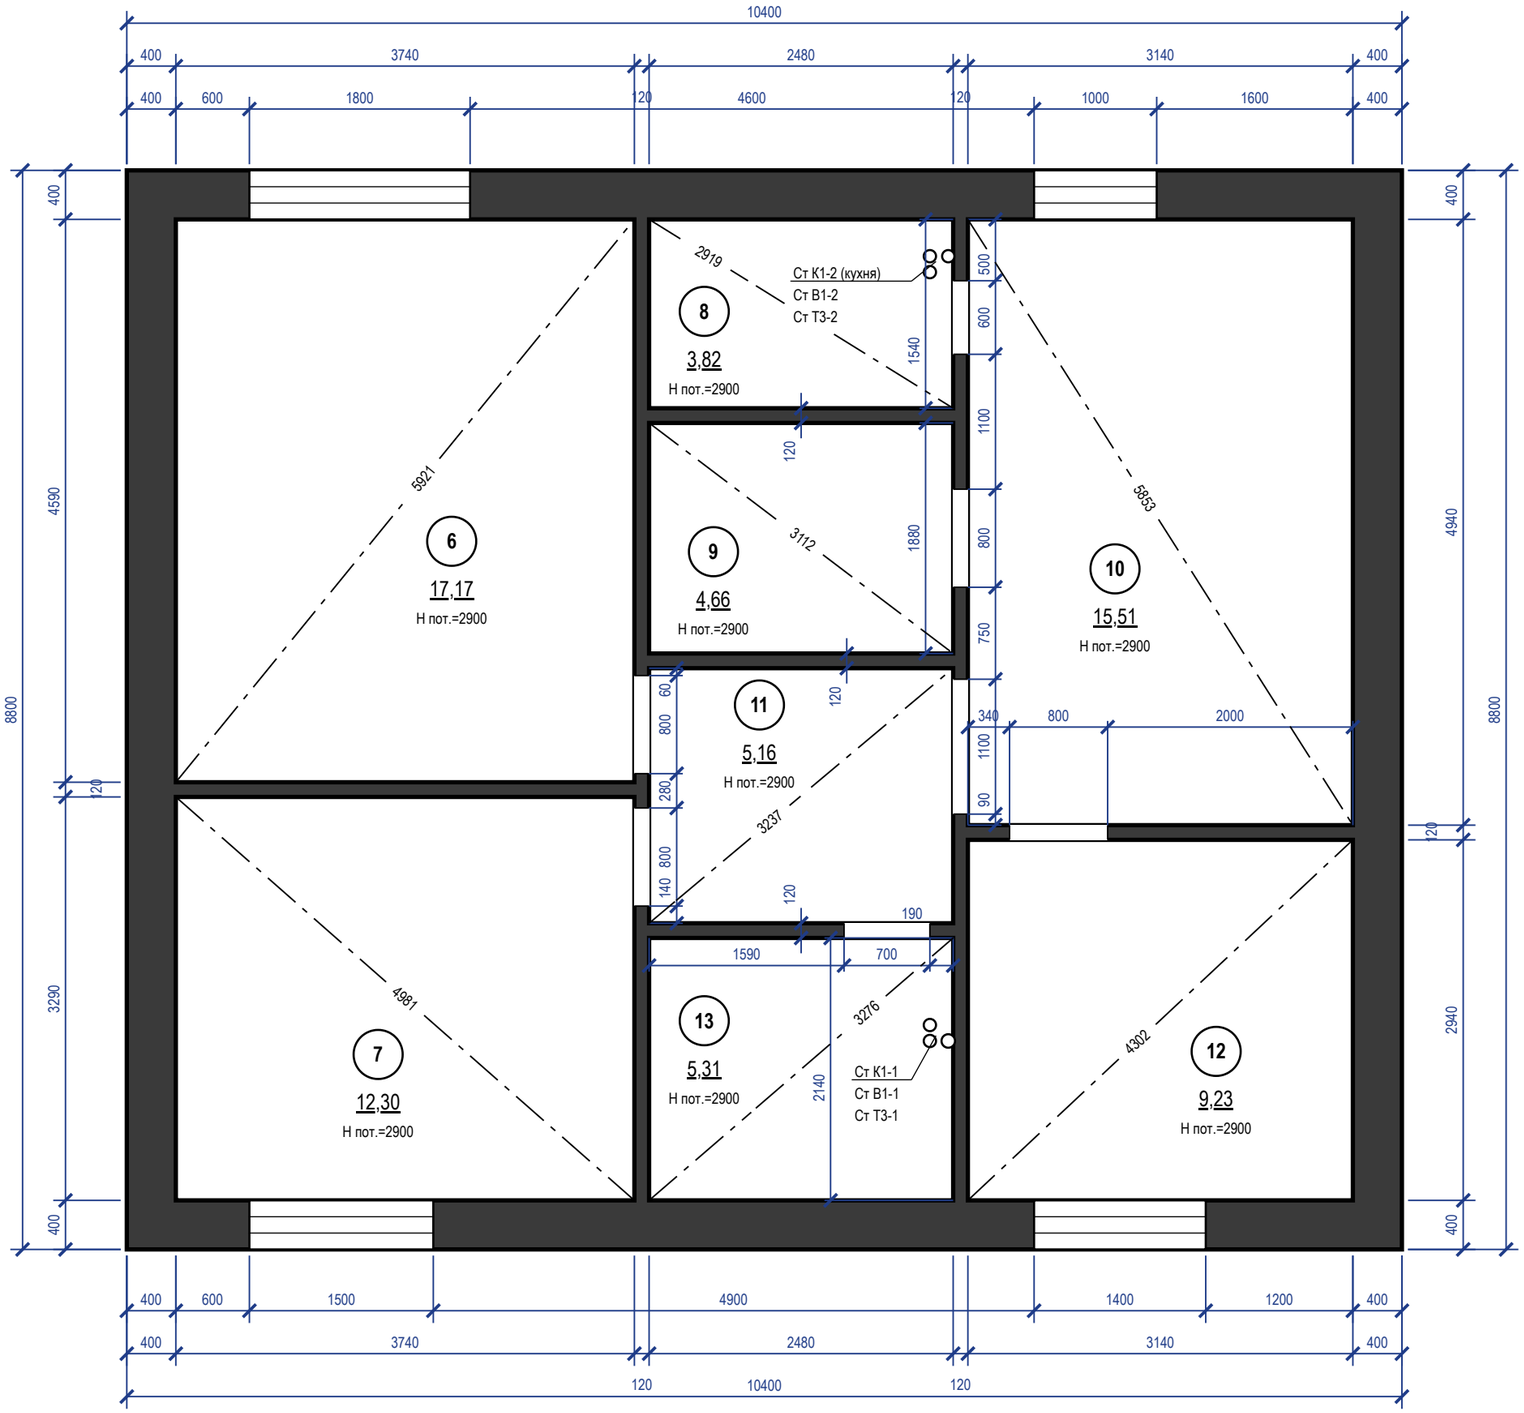

Экспликация помещений

№	Наименование	Площадь, м²
6	Спальня родителей	17,17
7	Детская	12,30
8	Гардеробная	3,82
9	Кладовая	4,66
10	Холл второго этажа	15,51
11	Коридор второго этажа	5,16
12	Детская вторая	9,23
13	Санузел второго этажа	5,31
	Итого (общая площадь)	**147,36**

Условные обозначения

- существующие стены (сечение)
- окно (рама, остекление)
- проём существующий, без заполнения (откосы)
- стояк: К1 — канализация, В1 — ХВС, Т3 — ГВС
- диагональ помещения — контроль прямоугольности
- (1) номер помещения, площадь м²

Примечания

1. Размеры — в мм по чистым поверхностям стен до отделки (по плану заказчика); площади — в м² по тем же размерам. До начала работ выполнить контрольный обмер.
2. За отметку ±0,000 принят чистый пол, не существующий (блок отметок). Н пот. высота от чистого пола до плиты перекрытия.
3. Толщины стен: наружные 400 мм, перегородки 120 мм; отличающиеся толщины и уступы — размерами на плане.
4. Несущие стены не определены: до технического заключения все стены считать несущими; проёмы и штробы в них не выполнять.
5. Дверные проёмы показаны без заполнения; высота дверных проёмов 2100 мм, проёмов без двери 2100 мм; низ окон (подоконник) 900 мм от чистого пола, высота окон 1500, 1450 мм.
6. Диагонали — контрольные размеры; расхождение более 5 мм подписать на плане как перекос.
7. Размеры проверить на месте до начала работ; расхождение контрольных промеров ≤ 2 %.

Отметки по высоте

±0,000	чистый пол пом. 6–12; отсчёт высот
−0,015	чистый пол пом. 13, ниже на 15 мм
−0,064	верх плиты — расчёт, не замер (задание на обмер)
сущ. пол	снимается до плиты; не замерен (задание на обмер)

	Лист	№ док.	Подпись	Дата
Дизайнер	Кырлан А.С.			19.10.26

Проект: Дом 120 м²


План планировки от заказчика · 2-й этаж

Стадия	Лист	Листов
П	4	128

выпуск 19.10.2026 № 66b2a77b4d · стр. 4 из 128

Экспликация помещений

№	Наименование	Площадь, м²
1	Гостиная-кухня	31,32
2	Холл с лестницей	15,51
3	Кабинет	11,00
4	Санузел гостевой	4,17
5	Прихожая	12,20
	Итого (общая площадь)	**147,36**

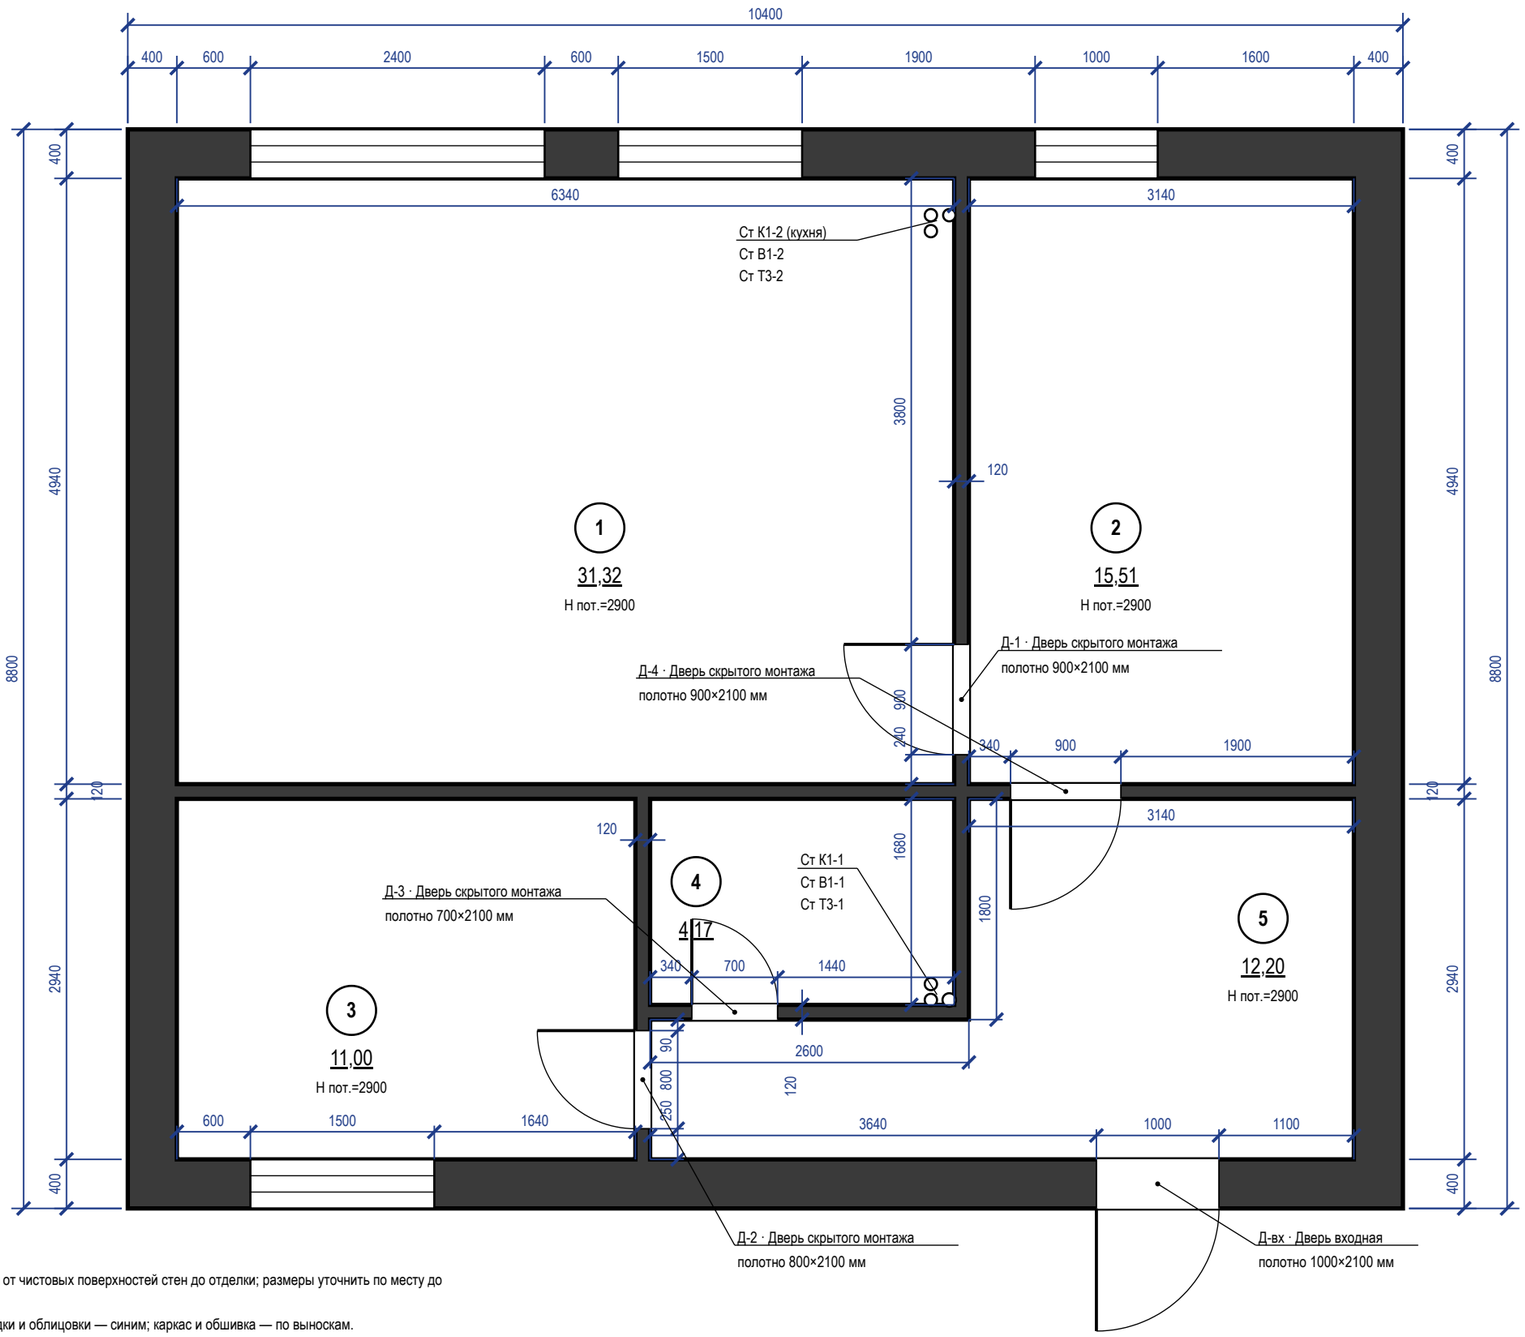

Примечания

1. Размеры — в мм от чистовых поверхностей стен до отделки; размеры уточнить по месту до начала работ.
2. Новые перегородки и облицовки — синим; каркас и обшивка — по выноскам.
3. Несущие стены не изменять: проёмы, ниши и штробы в них — только по техническому заключению.


					Проект: Дом 120 м²
	Лист	№ док.	Подпись	Дата	
Дизайнер	Кырлан А.С.			19.10.26	План монтажный · 1-й этаж

Стадия	Лист	Листов
П	5	128

выпуск 19.10.2026 № 66b2a77b4d · стр. 5 из 128

Экспликация помещений

№	Наименование	Площадь, м²
6	Спальня родителей	17,17
7	Детская	12,30
8	Гардеробная	3,82
9	Кладовая	4,66
10	Холл второго этажа	15,51
11	Коридор второго этажа	5,16
12	Детская вторая	9,23
13	Санузел второго этажа	5,31
	Итого (общая площадь)	**147,36**

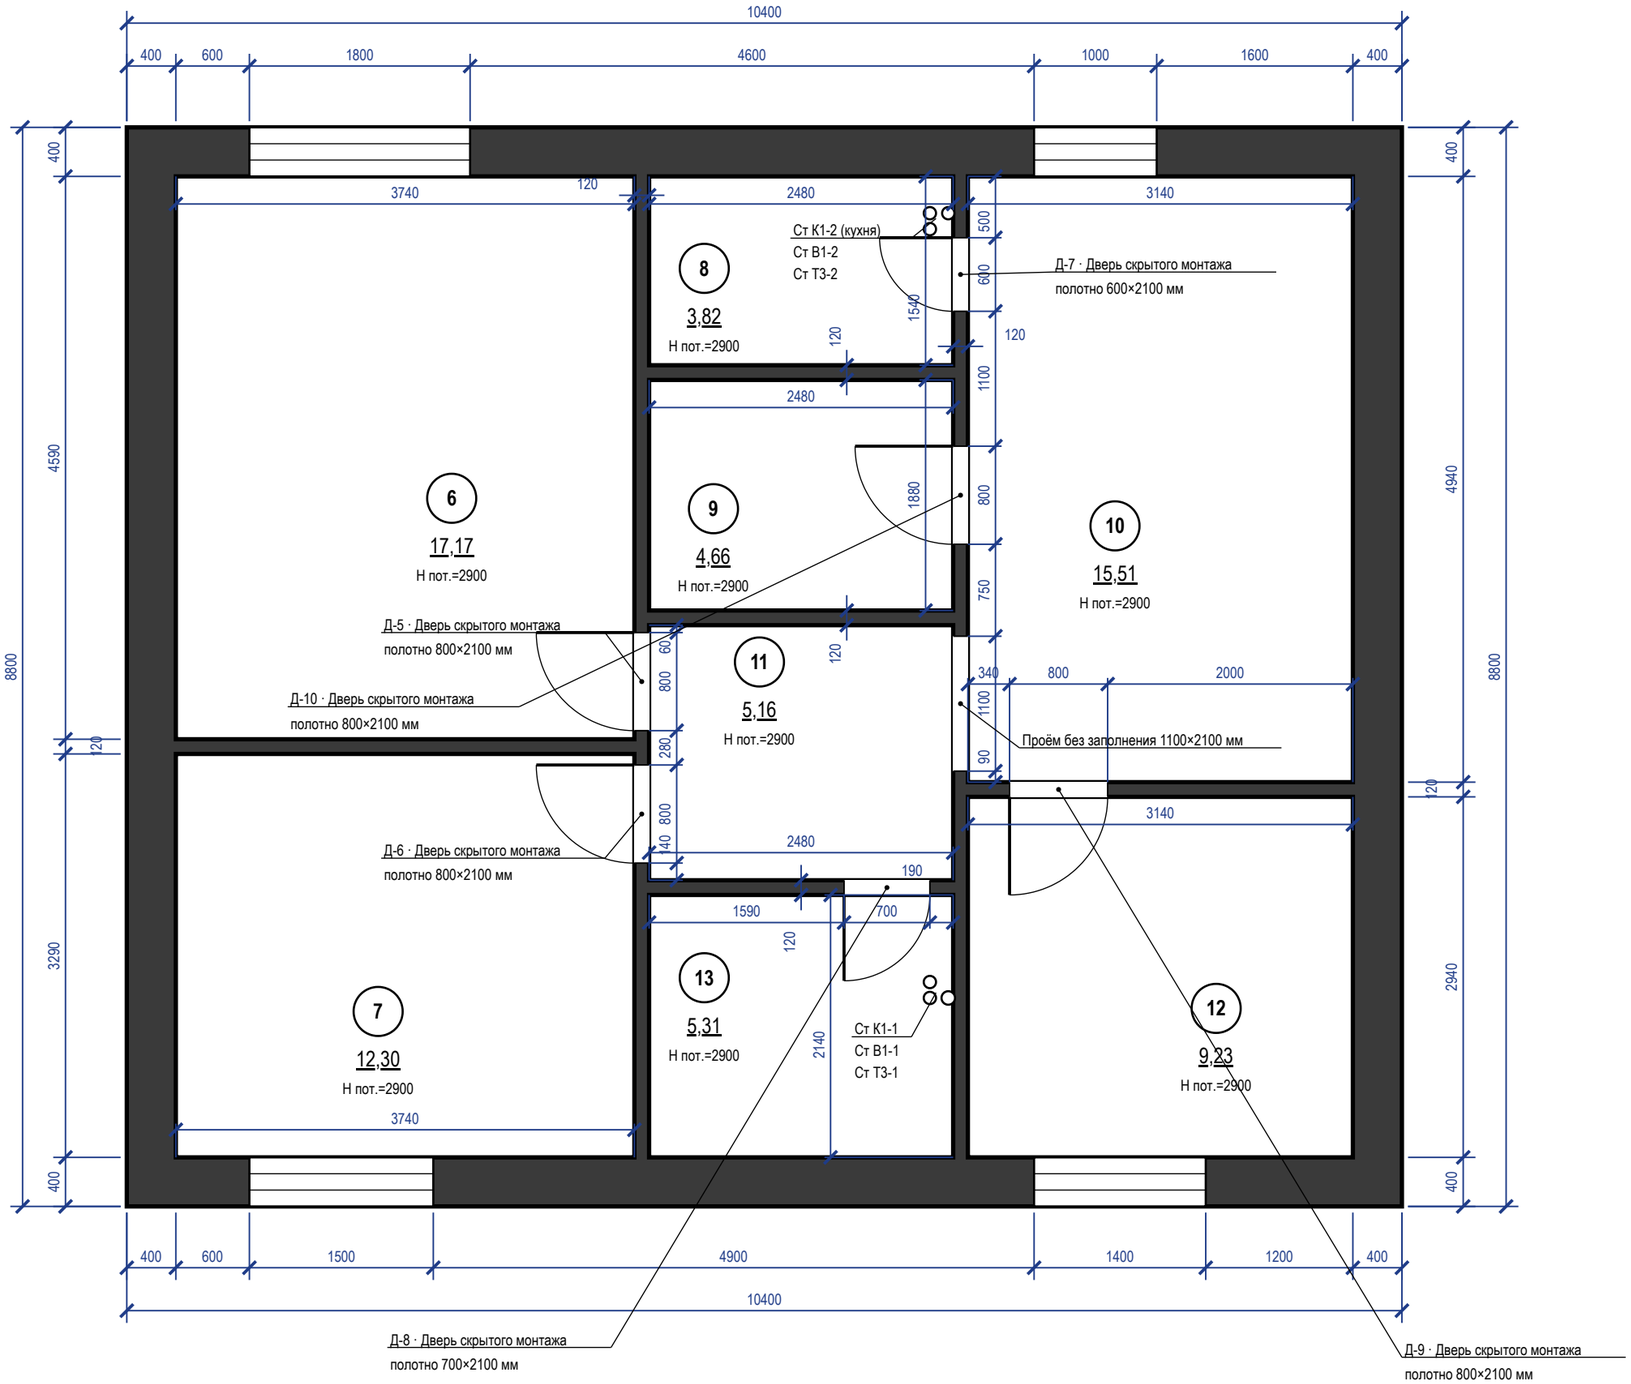

Примечания


1. Размеры — в мм от чистовых поверхностей стен до отделки; размеры уточнить по месту до начала работ.
2. Новые перегородки и облицовки — синим; каркас и обшивка — по выноскам.
3. Несущие стены не изменять: проёмы, ниши и штробы в них — только по техническому заключению.

					Проект: Дом 120 м²
	Лист	№ док.	Подпись	Дата	План монтажный · 2-й этаж
Дизайнер	Кырлан А.С.			19.10.26	


Стадия	Лист	Листов
П	6	128

выпуск 19.10.2026 № 66b2a77b4d · стр. 6 из 128

Привязка выводов и крепление модулей

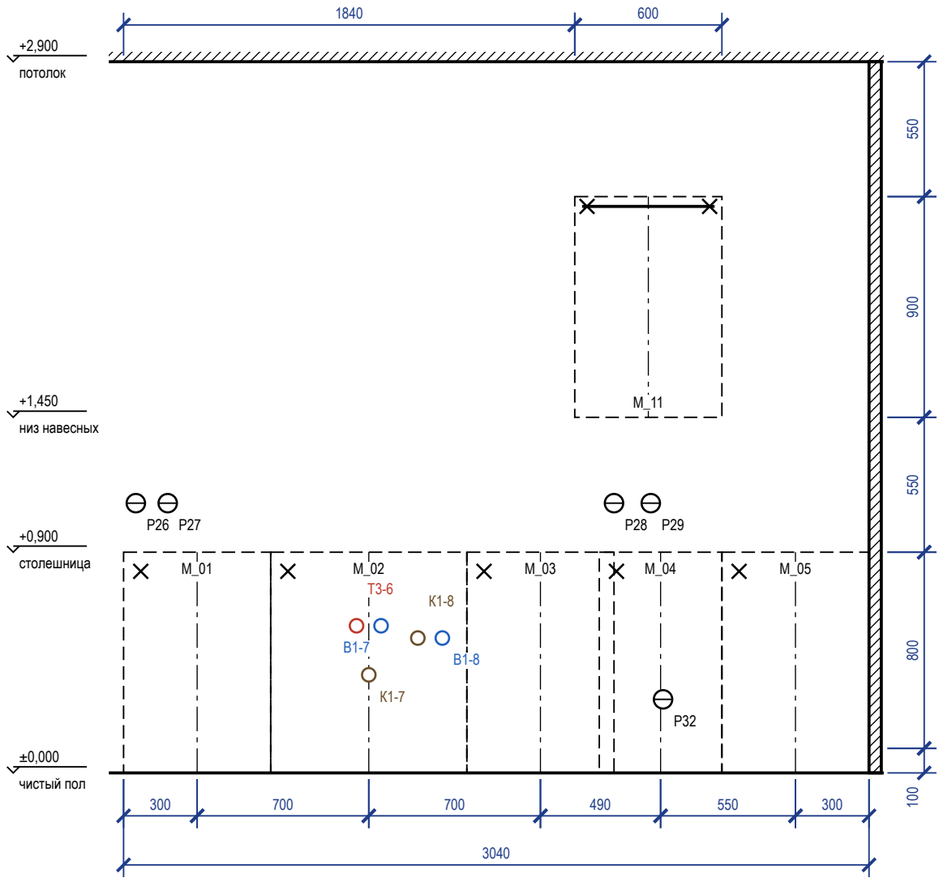

План столешницы

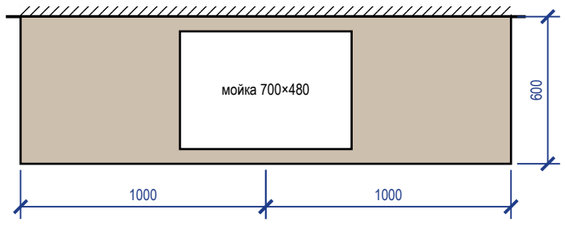

Привязка выводов к осям модулей

Код	Назначение	Модуль	От оси, мм	H, мм	Размещение
P26	розетка ×2 — фартук	M_01	−250	1100	над столешницей (фартук)
P27	розетка — фартук	M_01	−120	1100	над столешницей (фартук)
T3-6	T3 — межос. 100	M_02	−50	600	в модуле мойки
K1-7	K1 Ø50 — мойка	M_02	0	400	в модуле мойки
B1-7	B1 — межос. 100	M_02	+50	600	в модуле мойки
K1-8	K1 Ø40 — слив ПММ в шкафу мойки	M_02	+200	550	в модуле мойки
B1-8	B1 — кран ПММ в шкафу мойки	M_02	+300	550	в модуле мойки
P28	розетка ×2 — фартук	M_03	+300	1100	над столешницей (фартук)
P29	розетка — фартук	M_04	−40	1100	над столешницей (фартук)
P32	розетка — посудомоечная машина	M_04	+10	300	в соседнем модуле, за ящиком

Зазоры под отделку

Поверхность	Отделка	Зазор, мм	Учесть
фартук	керамогранит	10	от чернового основания до корпуса навесных и столешницы
стены	окраска	5	под штукатурку и шпаклёвку за пеналом
пол	инженерная доска		цоколь — после укладки пола, опоры ±20 мм

Условные обозначения

- навесной модуль (невидимый контур)
- ось модуля (от неё — привязка вывода)
- анкер / уголок крепления к стене
- розетка на стене
- вывод кабеля к технике
- B1 — вывод воды B1 / T3, канализации K1


Примечания

1. Выводы — по проекту электрики и ВК; привязка по горизонтали — от оси модуля (плюс — вправо по виду), по высоте — от чистого пола до оси вывода.
2. Пенал — уголки к стене 2 шт. сверху; нижние модули — стяжками между собой и уголком к стене; ряд выставить по уровню опорами цоколя.
3. Розетки над столешницей — не ниже 150 мм над ней и не за корпусом техники; розетка за ПММ, духовым шкафом и холодильником — только в соседнем модуле или в зоне цоколя с доступом.
4. Столешница — вырезы по шаблонам выбранных моделей мойки и варочной панели; торцы у стены — герметик, пристеночный плинтус.


					Проект: Дом 120 м²
	Лист	№ док.	Подпись	Дата	Кухня (пом. 1). Монтажная схема
Дизайнер	Кырлан А.С.			19.10.26	Стадия: П; Лист: 7; Листов: 128

выпуск 19.10.2026 № 66b2a77b4d · стр. 7 из 128

Привязка выводов и крепление модулей

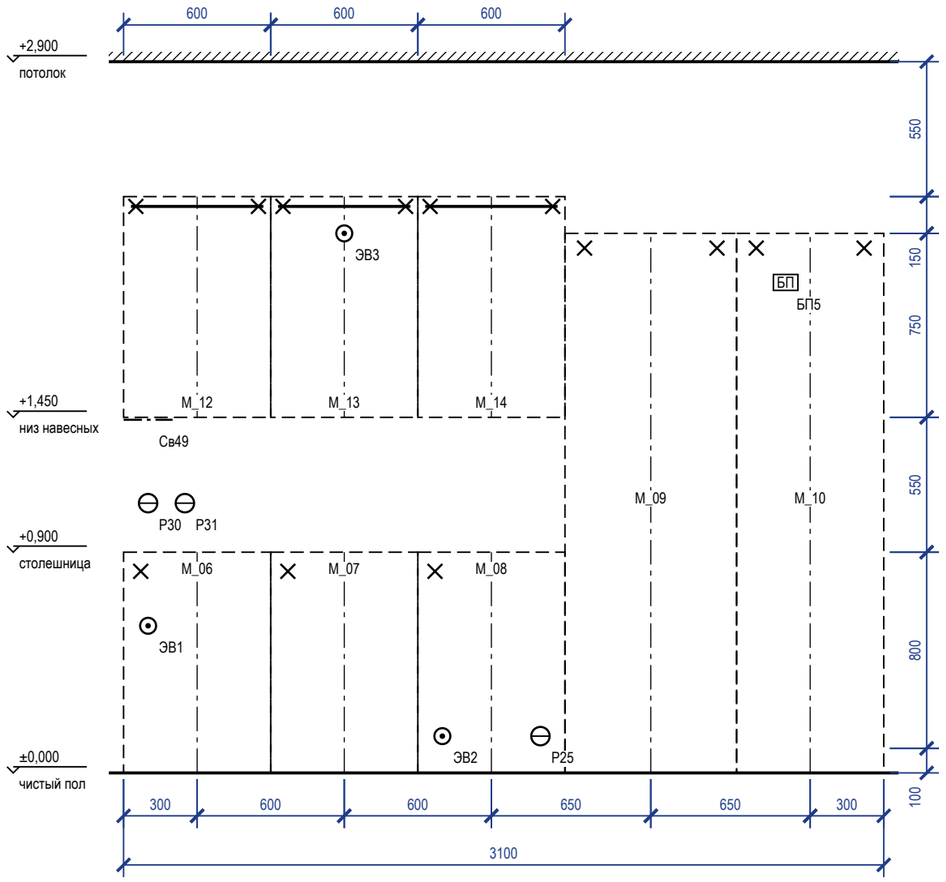

План столешницы

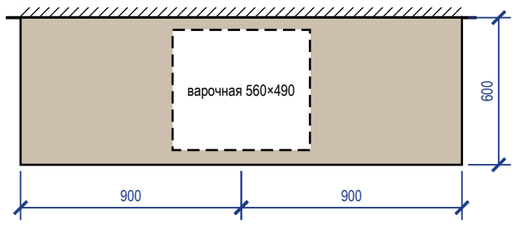

Привязка выводов к осям модулей

Код	Назначение	Модуль	От оси, мм	H, мм	Размещение
Р30	розетка ×2 — фартук между мойкой и варочной	М_06	−200	1100	над столешницей (фартук)
ЭВ1	вывод кабеля — варочная панель (в соседнем модуле М8.3, за ящиком)	М_06	−200	600	в соседнем модуле, за ящиком
Св49	светодиодная лента — подсветка столешницы	М_06	−200	1440	в профиле по низу навесного модуля
Р31	розетка — фартук между мойкой и варочной	М_06	−50	1100	над столешницей (фартук)
ЭВ3	вывод кабеля — вытяжка	М_13	0	2200	в навесном модуле
ЭВ2	вывод кабеля — духовой шкаф	М_08	−200	150	в соседнем модуле, за ящиком
Р25	розетка — холодильник М_09 (розетка в соседнем модуле М_08, съёмная панель)	М_08	+200	150	в соседнем модуле, за ящиком
БП5	блок питания — в пенале М_32, верх, съёмная панель	М_10	−100	2000	за пеналом

Зазоры под отделку

Поверхность	Отделка	Зазор, мм	Учесть
фартук	керамогранит	10	от чернового основания до корпуса навесных и столешницы
стены	окраска	5	под штукатурку и шпаклёвку за пеналом
пол	инженерная доска		цоколь — после укладки пола, опоры ±20 мм

Условные обозначения

- навесной модуль (невидимый контур)
- ось модуля (от неё — привязка вывода)
- анкер / уголок крепления к стене
- розетка на стене
- вывод кабеля к технике
- B1 — вывод воды В1 / Т3, канализации К1


Примечания

1. Выводы — по проекту электрики и ВК; привязка по горизонтали — от оси модуля (плюс — вправо по виду), по высоте — от чистого пола до оси вывода.
2. Пенал — уголки к стене 2 шт. сверху; нижние модули — стяжками между собой и уголком к стене; ряд выставить по уровню опорами цоколя.
3. Розетки над столешницей — не ниже 150 мм над ней и не за корпусом техники; розетка за ПММ, духовым шкафом и холодильником — только в соседнем модуле или в зоне цоколя с доступом.
4. Столешница — вырезы по шаблонам выбранных моделей мойки и варочной панели; торцы у стены — герметик, пристеночный плинтус.


					Проект: Дом 120 м²
	Лист	№ док.	Подпись	Дата	Кухня (пом. 1). Монтажная схема
Дизайнер	Кырлан А.С.			19.10.26	Стадия: П; Лист: 8; Листов: 128

выпуск 19.10.2026 № 66b2a77b4d · стр. 8 из 128


Шкаф-купе M_25 (пом. 5)

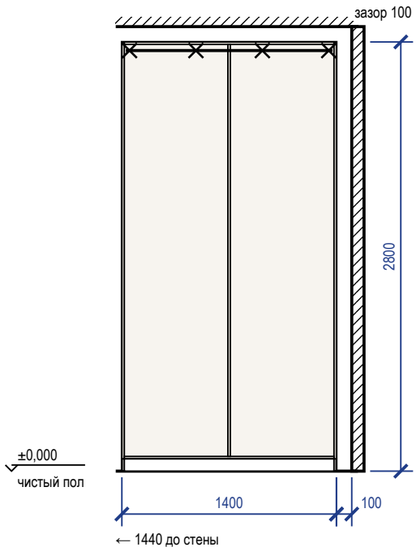


Шкаф распашной M_30 (пом. 6)

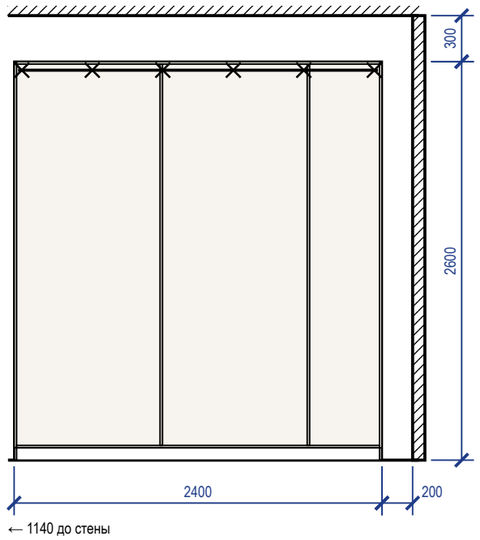


Шкаф распашной M_35 (пом. 7)

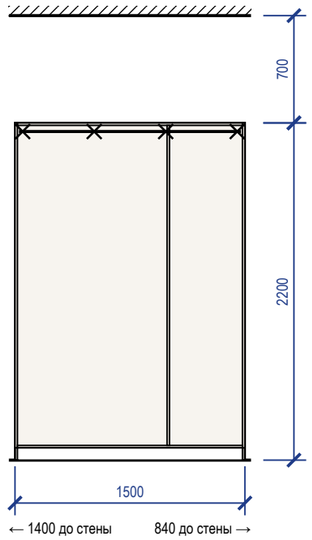

Система хранения M_38 (пом. 8)

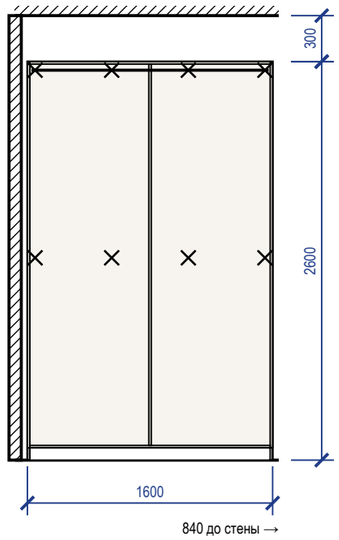

Система хранения M_39 пом. 8

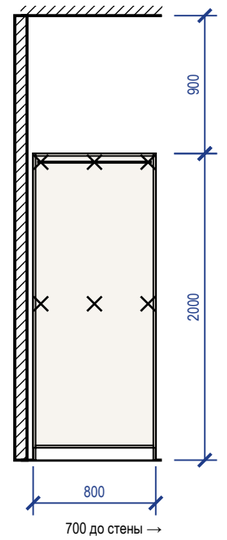

Крепление и зазоры под отделку (изделия листа 1)

Марка	Помещение, стена	Основание	Отделка стены	Зазор, мм	Крепёж по планке	От опрокидывания
M_25	Прихожая (5), стена Б	по основанию — см. таблицу крепежа	окраска	5	анкер 4 шт., шаг 433	уголки 2 шт.
M_30	Спальня родителей (6), стена В	по основанию — см. таблицу крепежа	окраска	5	анкер 6 шт., шаг 460	уголки 2 шт.
M_35	Детская (7), стена А	по основанию — см. таблицу крепежа	окраска	5	анкер 4 шт., шаг 467	уголки 2 шт.
M_38	Гардеробная (8), стена А	по основанию — см. таблицу крепежа	окраска	5	анкер 8 шт. (2 ряда)	true
M_39	Гардеробная (8), стена Г	по основанию — см. таблицу крепежа	окраска	5	анкер 6 шт. (2 ряда)	true

Крепёж по основанию стены

Основание стены	Крепёж
бетон, ж/б	анкер-шуруп 7,5×72 или дюбель 8×60 с шурупом 5×70
кирпич полнотелый	дюбель 8×80 с шурупом 5×90
газобетон, пазогребень	дюбель для газобетона 10×100 или химический анкер
гипсокартон	закладная до обшивки (брус 40×80 или фанера 18 мм), саморез в закладную

Условные обозначения

- анкер / уголок крепления к стене
- корпус и полки ЛДСП (вид на стену)
- компенсатор — короб до потолка


Примечания

1. Установочные размеры — от чистого пола и чистых стен; перед установкой контрольный замер после отделки.
2. Порядок: корпус выставить по уровню опорами цоколя → закрепить к стене по задней планке → навесить двери и фасады, отрегулировать зазоры → подогнать и закрепить компенсатор.
3. Анкеры — с шагом не более 500 мм, не ближе 50 мм от края планки; на ГКЛ только в закладную, установленную до обшивки.
4. Скрытые коммуникации под анкеры проверить детектором; трассы электрики по плану розеток.
5. Монтажная схема на 2 листах, лист 1 из 2; продолжение — на следующем листе схемы. Условные обозначения, таблица крепежа по основанию и примечания повторены на каждом листе.


					Проект: Дом 120 м²	
	Лист	№ док.	Подпись	Дата	Шкафы. Монтажная схема. Лист 1 из 2	Стадия / Лист / Листов
Дизайнер	Кырлан А.С.			19.10.26		П / 9 / 128

выпуск 19.10.2026 № 66b2a77b4d · стр. 9 из 128


Система хранения M_40 (пом. 9)

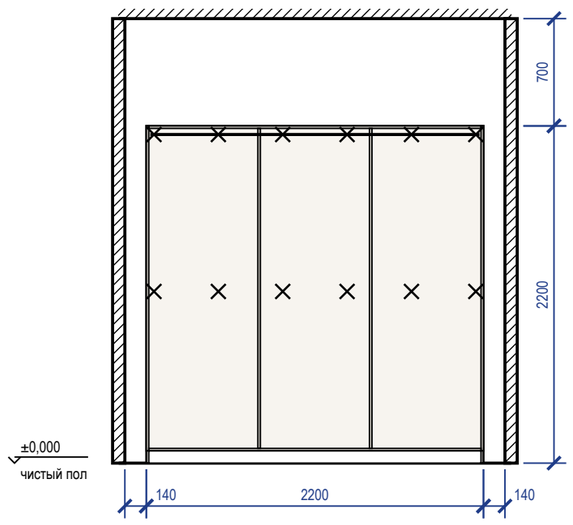


Система хранения M_41 пом. 9

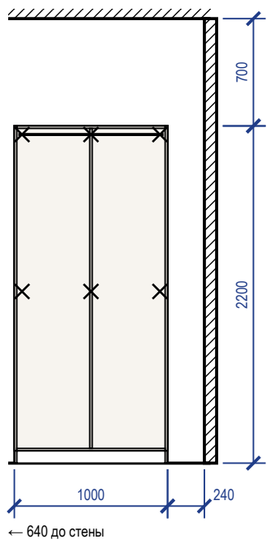

Шкаф распашной M_45 (пом. 12)

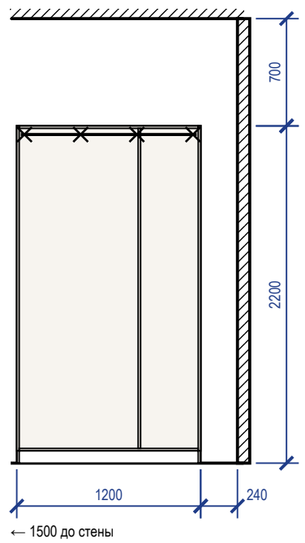

Система хранения M_47 пом. 12

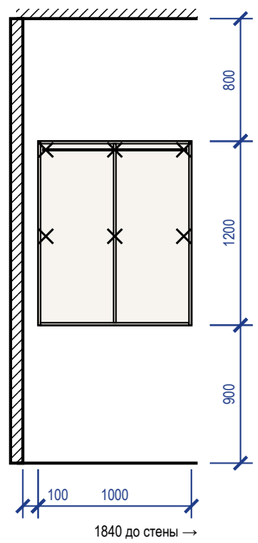

Крепление и зазоры под отделку (изделия листа 2)

Марка	Помещение, стена	Основание	Отделка стены	Зазор, мм	Крепёж по планке	От опрокидывания
M_40	Кладовая (9), стена В	по основанию — см. таблицу крепежа	окраска	5	анкер 12 шт. (2 ряда)	true
M_41	Кладовая (9), стена Г	по основанию — см. таблицу крепежа	окраска	5	анкер 6 шт. (2 ряда)	true
M_45	Детская вторая (12), стена Г	по основанию — см. таблицу крепежа	окраска	5	анкер 4 шт., шаг 367	уголки 2 шт.
M_47	Детская вторая (12), стена Г	по основанию — см. таблицу крепежа	окраска	5	анкер 6 шт. (2 ряда)	true

Крепёж по основанию стены

Основание стены	Крепёж
бетон, ж/б	анкер-шуруп 7,5×72 или дюбель 8×60 с шурупом 5×70
кирпич полнотелый	дюбель 8×80 с шурупом 5×90
газобетон, пазогребень	дюбель для газобетона 10×100 или химический анкер
гипсокартон	закладная до обшивки (брус 40×80 или фанера 18 мм), саморез в закладную

Условные обозначения


- анкер / уголок крепления к стене
- корпус и полки ЛДСП (вид на стену)
- компенсатор — короб до потолка

Примечания

1. Установочные размеры — от чистого пола и чистых стен; перед установкой контрольный замер после отделки.
2. Порядок: корпус выставить по уровню опорами цоколя → закрепить к стене по задней планке → навесить двери и фасады, отрегулировать зазоры → подогнать и закрепить компенсатор.
3. Анкеры — с шагом не более 500 мм, не ближе 50 мм от края планки; на ГКЛ только в закладную, установленную до обшивки.
4. Скрытые коммуникации под анкеры проверить детектором; трассы электрики по плану розеток.
5. Монтажная схема на 2 листах, лист 2 из 2. Условные обозначения, таблица крепежа по основанию и примечания повторены на каждом листе.

					Проект: Дом 120 м²	
	Лист	№ док.	Подпись	Дата	Шкафы. Монтажная схема. Лист 2 из 2	Стадия / Лист / Листов
Дизайнер	Кырлан А.С.			19.10.26		П / 10 / 128

выпуск 19.10.2026 № 66b2a77b4d · стр. 10 из 128

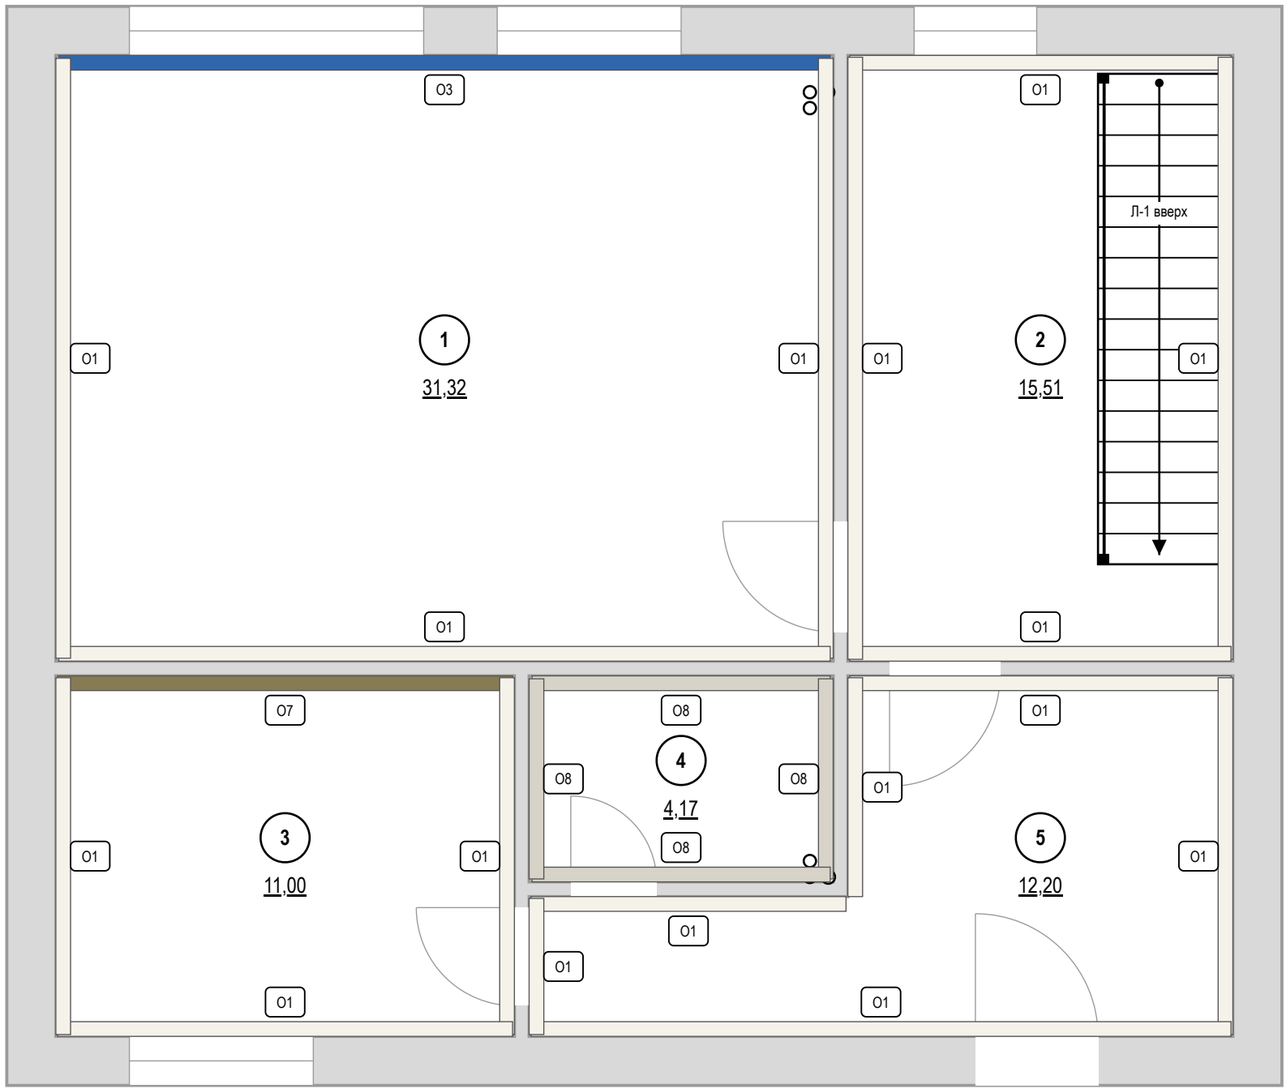


Покрытия стен

Марка	Покрытие	Помещение: S, м²	Итого, м²
О1	окраска Farrow & Ball · G503 «Calla»	1: 43,4; 2: 41,2; 3: 23,7; 5: 42,7	151,1
О3	окраска Farrow & Ball · S 3050-R80B «Эгейский синий»	1: 9,8	9,8
О7	окраска Farrow & Ball · S 5020-G90Y «Олива»	3: 10,8	10,8
О8	облицовка плиткой Atlas Concorde · A8UZ «Marvel Travertine» 600×1200 мм	4: 18,1	18,1

Площади — нетто, по развёрткам (за вычетом проёмов и фартука); высоты помещений — от чистого пола.

					Проект: Дом 120 м²
	Лист	№ док.	Подпись	Дата	
Дизайнер	Кырлан А.С.			19.10.26	Карта покрытий стен · 1-й этаж
					Стадия: П; Лист: 11; Листов: 128

выпуск 19.10.2026 № 66b2a77b4d · стр. 11 из 128

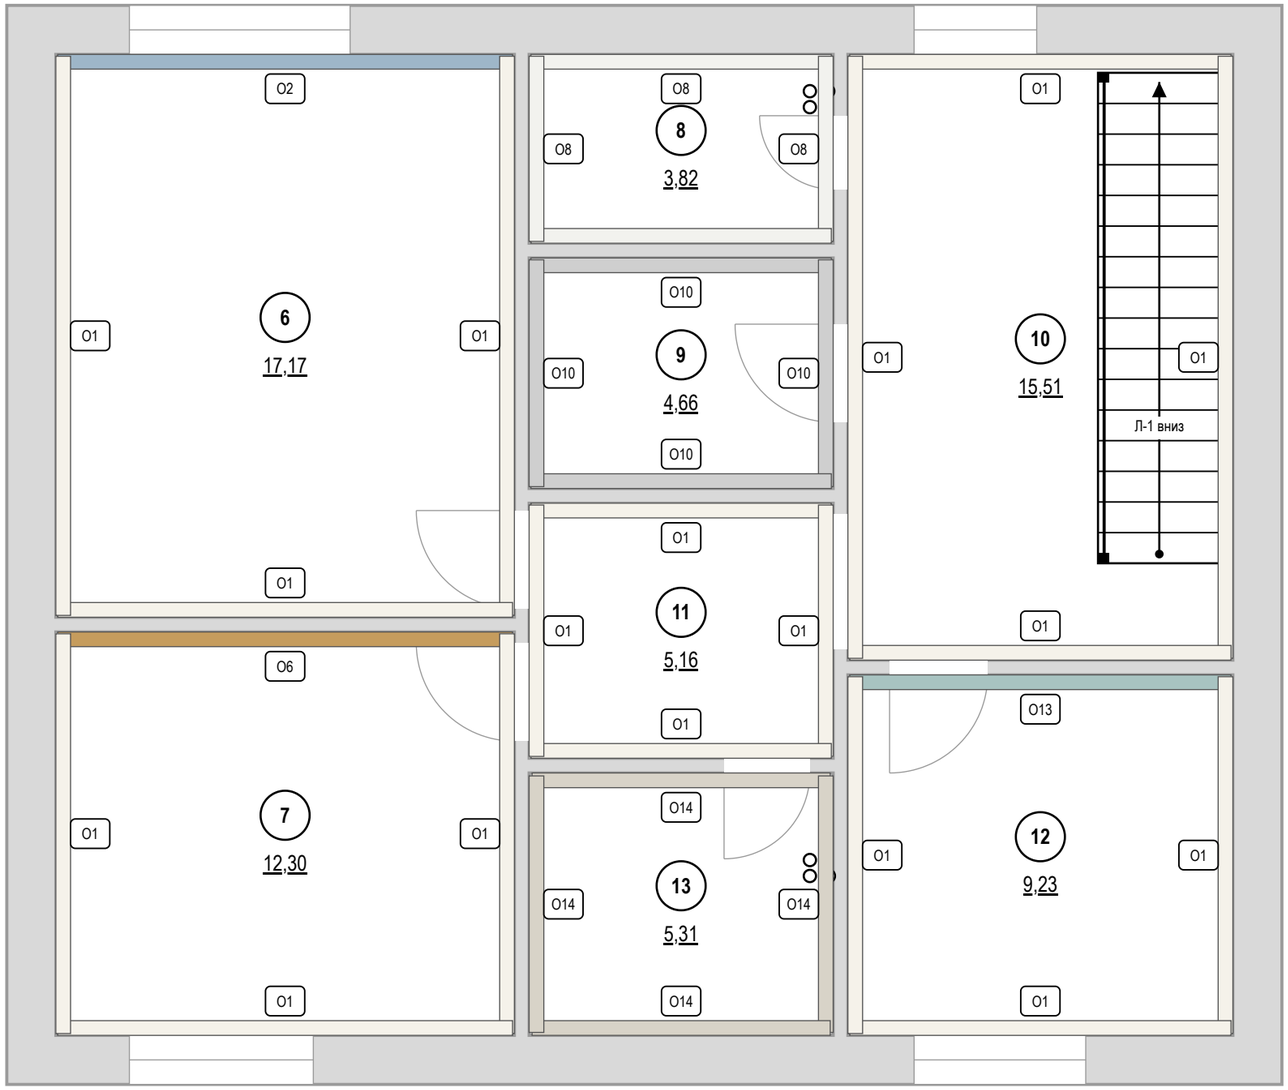

Покрытия стен

Марка	Покрытие	Помещение: S, м²	Итого, м²
O1	окраска Farrow & Ball · G503 «Calla»	6: 35,5; 7: 25,8; 10: 38,1; 11: 19,0; 12: 23,9	142,3
O2	окраска Farrow & Ball · No. 89 «Lulworth Blue — светлая морская лазурь»	6: 8,1	8,1
O6	окраска Farrow & Ball · No. 66 «India Yellow — охра / горчица итальянских фасадов»	7: 10,8	10,8
O8	окраска Tikkurila · No. 222 «Loft White»	8: 21,7	21,7
O10	окраска Tikkurila · S 0502-Y	9: 23,3	23,3
O13	окраска Farrow & Ball · H440 «H440 Wave — бирюзово-голубая вода»	12: 7,3	7,3
O14	облицовка плиткой Atlas Concorde · A8UZ «Marvel Travertine» 600×1200 мм	13: 20,3	20,3

					Проект: Дом 120 м²
	Лист	№ док.	Подпись	Дата	
Дизайнер	Кырлан А.С.			19.10.26	Карта покрытий стен · 2-й этаж

Стадия	Лист	Листов
П	12	128

выпуск 19.10.2026 № 66b2a77b4d · стр. 12 из 128

Колерная карта по помещениям

Помещение	Поверхность	Образец	Поз.	Система и код цвета	Производитель, линейка / материал, артикул	Блеск	Класс EN 13300	LRV	Площадь
1. Гостиная-кухня 31,32 м²	стены		**K1**	Tikkurila G503	Farrow & Ball · Modern Emulsion	матовая	1	89	43,1 м²
	акцент А		**K2**	NCS S 3050-R80B	Farrow & Ball · Modern Emulsion	матовая	1	≈13	11,6 м²
	потолок		**K3**	Little Greene No. 222	Tikkurila · Anti-Reflex 2	глубокомат.	2	92	31,3 м²
	пол		**KM1**	по образцу	Coswick · Вековые традиции				31,3 м²
	плинтус		**K4**	Tikkurila G503	МДФ · в цвет Tikkurila			89	21,7 м
	фартук		**KM2**	по образцу	керамогранит · аналог по хар.				2,0 м²
2. Холл с лестницей 15,51 м²	стены		**K1**	Tikkurila G503	Farrow & Ball · Modern Emulsion	матовая	1	89	41,6 м²
	потолок		**K3**	Little Greene No. 222	Tikkurila · Anti-Reflex 2	глубокомат.	2	92	15,5 м²
	пол		**KM1**	по образцу	Coswick · Вековые традиции				15,5 м²
	плинтус		**K4**	Tikkurila G503	МДФ · в цвет Tikkurila			89	14,4 м
3. Кабинет 11 м²	стены		**K1**	Tikkurila G503	Farrow & Ball · Modern Emulsion	матовая	1	89	24,0 м²
	акцент А		**K5**	NCS S 5020-G90Y	Farrow & Ball · Modern Emulsion	матовая	1	≈20	10,8 м²
	потолок		**K3**	Little Greene No. 222	Tikkurila · Anti-Reflex 2	глубокомат.	2	92	11,0 м²
	пол		**KM1**	по образцу	Coswick · Вековые традиции				11,0 м²
	плинтус		**K4**	Tikkurila G503	МДФ · в цвет Tikkurila			89	12,6 м
4. Санузел гостевой 4,17 м²	стены		**K6**	Atlas Concorde A8UZ	Atlas Concorde · Marvel Travertine				18,5 м²
	потолок		**K7**	Little Greene No. 222	Tikkurila · Luja 7	матовая	1	92	4,2 м²
	пол		**K6**	Atlas Concorde A8UZ	Atlas Concorde · Marvel Travertine				4,2 м²
5. Прихожая 12,2 м²	стены		**K1**	Tikkurila G503	Farrow & Ball · Modern Emulsion	матовая	1	89	43,2 м²
	потолок		**K3**	Little Greene No. 222	Tikkurila · Anti-Reflex 2	глубокомат.	2	92	12,2 м²
	пол		**K6**	Atlas Concorde A8UZ	Atlas Concorde · Marvel Travertine				12,2 м²
	плинтус		**K4**	Tikkurila G503	МДФ · в цвет Tikkurila			89	14,0 м

Перечень выкрасов на согласование

№	Код	Бренд / веер	Пом. / стена	Подложка	Формат	Статус
1	G503	Tikkurila	1, 2, 3, 5	ГКЛ, загрунтованный под эту краску; МДФ, загрунтованный под эмаль	600×1000; 300×600	к выполнению
2	S 3050-R80B	NCS Farrow & Ball	1 A	ГКЛ, загрунтованный под эту краску	600×1000	к выполнению
3	No. 222	Little Greene	1, 2, 3, 4, 5	ГКЛ, загрунтованный под эту краску	600×1000	к выполнению
4	S 5020-G90Y	NCS Farrow & Ball	3 A	ГКЛ, загрунтованный под эту краску	600×1000	к выполнению

Примечания

1. Цвет утверждается только по выкрасу на объекте: формат от А3 до 1000×1000 мм на загрунтованном ГКЛ, в 2 слоя (как на стене), не на белой шпаклёвке; смотреть днём и при свете проекта своего помещения, рядом с образцами пола и фасадов. Подпись на обороте: код, бренд и веер, дата.
2. Колеровка машинная в колеровочном центре бренда; каждый код — за один проход, одной партией на весь объём. Колеровщику передаётся только система и код утверждённого веера; плашки и HEX на листе — ориентир, печать не является эталоном цвета.
3. Класс мокрого истирания — EN 13300 (ISO 11998); блеск — по ГОСТ 31975 (ISO 2813), геометрия 60°. LRV — пересчёт координаты L каталога производителя (Y = ((L*+16)/116)³); «≈» — расчёт по HEX, справочно.
4. Площади поверхностей — тем же способом и с теми же цифрами, что в ведомости отделки (способ счёта — в общих указаниях); объём краски к заказу, фасовка и материалы КМ — в спецификации отделочных материалов.
5. Перечень выкрасов составлен по кодам колерной карты; к основному тону стен добавить на выкрас 2 соседних тона того же веера (светлее и темнее), статус отмечать в графе «Статус» при согласовании.

Схема квартиры: цвет стен и акценты (б/м)

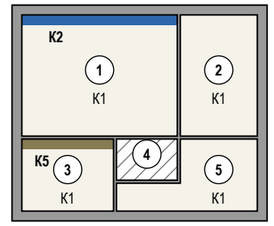


Схема палитры проекта

Стиль: Средиземноморский 60% + Скандинавский 40% · схема: complement

основной	основной	основной	второстепенный	второстепенный	второстепенный	акцентный	акцентный	акцентный
Tikkurila G503	**Farrow & Ball No. 239**	**Little Greene No. 222**	**NCS S 1010-Y20R**	**Farrow & Ball No. 89**	**Farrow & Ball No. 292**	**NCS S 3050-R80B**	**Farrow & Ball No. 66**	**NCS S 5020-G90Y**
Calla LRV 89 стены 1,2,3,5; плинтус 1,2,3,5	Wimborne White – белый с каплей тёплой охры LRV ≈89 в отделке не применён	Loft White LRV 92 потолок 1,2,3,4,5; текстиль/декор 1,3	Светлый песок / известняк LRV 75 текстиль/декор 1,3	Lulworth Blue – светлая морская лазурь LRV ≈45 в отделке не применён	Treron – серо-оливковая листва LRV 15 в отделке не применён	Эгейский синий LRV ≈13 акцент 1; текстиль/декор 1	India Yellow – охра	горчица итальянских фасадов LRV 36 в отделке не применён	Олива LRV ≈20 акцент 3; текстиль/декор 3

План 60/30/10



Окраска, факт — по площади стен, акцентов, потолков



окрашено всего 267,1 м²; второстепенный тон несут мебель и текстиль

Текстиль и декор в цветах вне палитры проекта

Tikkurila X463 X463 Sandstone — песчаник — пом. 1 (T15, T16, T19), 3 (T9)

Условные обозначения

K1 Tikkurila G503 · Calla · Modern Emulsion · матовая · кл. 1

K2 NCS S 3050-R80B · Эгейский синий · Farrow & Ball Modern Emulsion · матовая · кл. 1

K3 Little Greene No. 222 · Loft White · Anti-Reflex 2 · глубокомат. · кл. 2

K4 Tikkurila G503 · Calla · МДФ

K5 NCS S 5020-G90Y · Олива · Farrow & Ball Modern Emulsion · матовая · кл. 1

K6 Atlas Concorde A8UZ · Marvel Travertine · Marvel Travertine

K7 Little Greene No. 222 · Loft White · Luja 7 · матовая · кл. 1

KM1 инженерная доска · 1167-4250

KM2 аналог: керамогранит под травертин, матовый, 1200×600×9 мм

дерево (доска, паркет, ламинат) — рисунок досок

керамогранит, плитка, камень — сетка швов по формату

HEX не задан — цвет только по коду и вееру

К — позиция окраски (код + продукт + блеск), КМ — позиция материала, тон КМ — по описанию артикула, эталон — образец материала; ≈ LRV — расчёт по HEX, справочно

					Проект: Дом 120 м²
	Лист	№ док.	Подпись	Дата	Колерная карта · 1-й этаж
Дизайнер	Кырлан А.С.			19.10.26	

Стадия	Лист	Листов
П	13	128

выпуск 19.10.2026 № 66b2a77b4d · стр. 13 из 128

Колерная карта по помещениям

Помещение	Поверхность	Образец	Поз.	Система и код цвета	Производитель, линейка / материал, артикул	Блеск	Класс EN 13300	LRV	Площадь
6. Спальня родителей 17,17 м²	стены		**K1**	Tikkurila G503	Farrow & Ball · Modern Emulsion	матовая	1	89	35,8 м²
	акцент А		**K2**	Farrow & Ball No. 89	Farrow & Ball · Modern Emulsion	матовая	1	≈45	8,1 м²
	потолок		**K3**	Little Greene No. 222	Tikkurila · Anti-Reflex 2	глубокомат.	2	92	17,2 м²
	пол		**KM1**	по образцу	Coswick · Вековые традиции				17,2 м²
	плинтус		**K4**	Tikkurila G503	МДФ · в цвет Tikkurila			89	15,9 м
7. Детская 12,3 м²	стены		**K1**	Tikkurila G503	Farrow & Ball · Modern Emulsion	матовая	1	89	26,1 м²
	акцент А		**K5**	Farrow & Ball No. 66	Farrow & Ball · Modern Emulsion	матовая	1	36	10,8 м²
	потолок		**K3**	Little Greene No. 222	Tikkurila · Anti-Reflex 2	глубокомат.	2	92	12,3 м²
	пол		**KM1**	по образцу	Coswick · Вековые традиции				12,3 м²
	плинтус		**K6**	Tikkurila G503	Orac Decor · Contour (Luxxus)			89	13,3 м
8. Гардеробная 3,82 м²	стены		**K7**	Little Greene No. 222	Tikkurila · Harmony	матовая	1	92	22,1 м²
	потолок		**K3**	Little Greene No. 222	Tikkurila · Anti-Reflex 2	глубокомат.	2	92	3,8 м²
	пол		**KM1**	по образцу	Coswick · Вековые традиции				3,8 м²
	плинтус		**K8**	Little Greene No. 222	МДФ · в цвет Little Greene			92	7,4 м
9. Кладовая 4,66 м²	стены		**K9**	NCS S 0502-Y	Tikkurila	матовая	2	86	23,6 м²
	потолок		**K10**	NCS S 0300-N	Tikkurila	глубокомат.	2	92	4,7 м²
	пол		**KM1**	по образцу	Coswick · Вековые традиции				4,7 м²
	плинтус		**K11**	NCS S 0300-N	Orac Decor · Contour (Luxxus)	полуматов.		92	7,9 м
10. Холл второго этажа 15,51 м²	стены		**K1**	Tikkurila G503	Farrow & Ball · Modern Emulsion	матовая	1	89	38,4 м²
	потолок		**K3**	Little Greene No. 222	Tikkurila · Anti-Reflex 2	глубокомат.	2	92	15,5 м²
	пол		**KM1**	по образцу	Coswick · Вековые традиции				15,5 м²
	плинтус		**K4**	Tikkurila G503	МДФ · в цвет Tikkurila			89	12,9 м
11. Коридор второго этажа 5,16 м²	стены		**K1**	Tikkurila G503	Farrow & Ball · Modern Emulsion	матовая	1	89	19,3 м²
	потолок		**K3**	Little Greene No. 222	Tikkurila · Anti-Reflex 2	глубокомат.	2	92	5,2 м²
	пол		**KM1**	по образцу	Coswick · Вековые традиции				5,2 м²
	плинтус		**K4**	Tikkurila G503	МДФ · в цвет Tikkurila			89	5,7 м
12. Детская вторая 9,23 м²	стены		**K1**	Tikkurila G503	Farrow & Ball · Modern Emulsion	матовая	1	89	24,1 м²
	акцент А		**K12**	Tikkurila H440	Farrow & Ball · Modern Emulsion	матовая	1	≈51	7,4 м²
	потолок		**K3**	Little Greene No. 222	Tikkurila · Anti-Reflex 2	глубокомат.	2	92	9,2 м²
	пол		**KM1**	по образцу	Coswick · Вековые традиции				9,2 м²
	плинтус		**K6**	Tikkurila G503	Orac Decor · Contour (Luxxus)			89	11,4 м
13. Санузел второго этажа 5,31 м²	стены		**K13**	Atlas Concorde A8UZ	Atlas Concorde · Marvel Travertine				20,7 м²
	потолок		**K14**	Little Greene No. 222	Tikkurila · Luja 7	матовая	1	92	5,3 м²
	пол		**K13**	Atlas Concorde A8UZ	Atlas Concorde · Marvel Travertine				5,3 м²

Примечания

1. Цвет утверждается только по выкрасу на объекте: формат от А3 до 1000×1000 мм на загрунтованном ГКЛ, в 2 слоя (как на стене), не на белой шпаклёвке; смотреть днём и при свете проекта своего помещения, рядом с образцами пола и фасадов. Подпись на обороте: код, бренд и веер, дата.
2. Колеровка машинная в колеровочном центре бренда; каждый код — за один проход, одной партией на весь объём. Колеровщику передаётся только система и код утверждённого веера; плашки и HEX на листе — ориентир, печать не является эталоном цвета.
3. Класс мокрого истирания — EN 13300 (ISO 11998); блеск — по ГОСТ 31975 (ISO 2813), геометрия 60°. LRV — пересчёт координаты L каталога производителя (Y = ((L*+16)/116)³); «≈» — расчёт по HEX, справочно.
4. Площади поверхностей — тем же способом и с теми же цифрами, что в ведомости отделки (способ счёта — в общих указаниях); объём краски к заказу, фасовка и материалы КМ — в спецификации отделочных материалов.
5. Перечень выкрасов составлен по кодам колерной карты; к основному тону стен добавить на выкрас 2 соседних тона того же веера (светлее и темнее), статус отмечать в графе «Статус» при согласовании.

Схема палитры проекта


Стиль: Средиземноморский 60% + Скандинавский 40% · схема: complement

основной	основной	основной	второстепенный	второстепенный	второстепенный	акцентный	акцентный	акцентный
Tikkurila G503	Farrow & Ball No. 239	Little Greene No. 222	NCS S 1010-Y20R	Farrow & Ball No. 89	Farrow & Ball No. 292	NCS S 3050-R80B	Farrow & Ball No. 66	NCS S 5020-G90Y
Calla LRV 89 стены 6,7,10,11,12; плинтус 6,7,10,11,12	Wimborne White – белый с каплей тёплой охры LRV ≈89 в отделке не применён	Loft White LRV 92 потолок 6,7,8,10,11,12,13; стены 8; плинтус 8; текстиль/декор 6,7,12	Светлый песок / известняк LRV 75 текстиль/декор 6,7,12	Lulworth Blue – светлая морская лазурь LRV ≈45 акцент 6; текстиль/декор 6	Treron – серо-оливковая листва LRV 15 в отделке не применён	Эгейский синий LRV ≈13 в отделке не применён	India Yellow – охра / горчица итальянских фасадов LRV 36 акцент 7; текстиль/декор 7	Олива LRV ≈20 в отделке не применён

План 60/30/10



Окраска, факт — по площади стен, акцентов, потолков

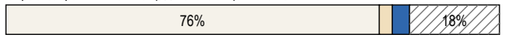

окрашено всего 309,7 м²; второстепенный тон несут мебель и текстиль

Текстиль и декор в цветах вне палитры проекта

- Tikkurila X395 X395 Playa — влажный пляжный песок — пом. 6 (T3)
- Tikkurila X463 X463 Sandstone — песчаник — пом. 7 (T22), 12 (T28)

Условные обозначения

- **K1** Tikkurila G503 · Calla · Modern Emulsion · матовая · кл. 1
- **K2** Farrow & Ball No. 89 · Lulworth Blue — светлая морская лазурь · Modern Emulsion · матовая · кл. 1
- **K3** Little Greene No. 222 · Loft White · Anti-Reflex 2 · глубокомат. · кл. 2
- **K4** Tikkurila G503 · Calla · МДФ
- **K5** Farrow & Ball No. 66 · India Yellow — охра / горчица итальянских фасадов · Modern Emulsion · матовая · кл. 1
- **K6** Tikkurila G503 · Calla · Contour (Luxxus)
- **K7** Little Greene No. 222 · Loft White · Harmony · матовая · кл. 1
- **K8** Little Greene No. 222 · Loft White · МДФ
- дерево (доска, паркет, ламинат) — рисунок досок
- HEX не задан — цвет только по коду и вееру
- **K9** NCS S 0502-Y · Tikkurila · матовая · кл. 2
- **K10** NCS S 0300-N · Tikkurila · глубокомат. · кл. 2
- **K11** NCS S 0300-N · Orac Decor Contour (Luxxus) · полуматов.
- **K12** Tikkurila H440 · H440 Wave — бирюзово-голубая вода · Modern Emulsion · матовая · кл. 1
- **K13** Atlas Concorde A8UZ · Marvel Travertine · Marvel Travertine
- **K14** Little Greene No. 222 · Loft White · Luja 7 · матовая · кл. 1
- **KM1** инженерная доска · 1167-4250

К — позиция окраски (код + продукт + блеск), КМ — позиция материала, тон КМ — по описанию артикула, эталон — образец материала; ≈ LRV — расчёт по HEX, справочно


Перечень выкрасов на согласование

№	Код	Бренд / веер	Пом. / стена	Подложка	Формат	Статус
1	G503	Tikkurila	6, 7, 10, 11, 12	ГКЛ, загрунтованный под эту краску; МДФ, загрунтованный под эмаль	600×1000; 300×600	к выполнению
2	No. 89	Farrow & Ball	6 А	ГКЛ, загрунтованный под эту краску	600×1000	к выполнению
3	No. 222	Little Greene	6, 7, 8, 10, 11, 12, 13	ГКЛ, загрунтованный под эту краску; МДФ, загрунтованный под эмаль	600×1000; 300×600	к выполнению

… ещё 4 выкрасов — в ведомости отделки

					Проект: Дом 120 м²
	Лист	№ док.	Подпись	Дата	Колерная карта · 2-й этаж
Дизайнер	Кырлан А.С.			19.10.26	

Стадия	Лист	Листов
П	14	128

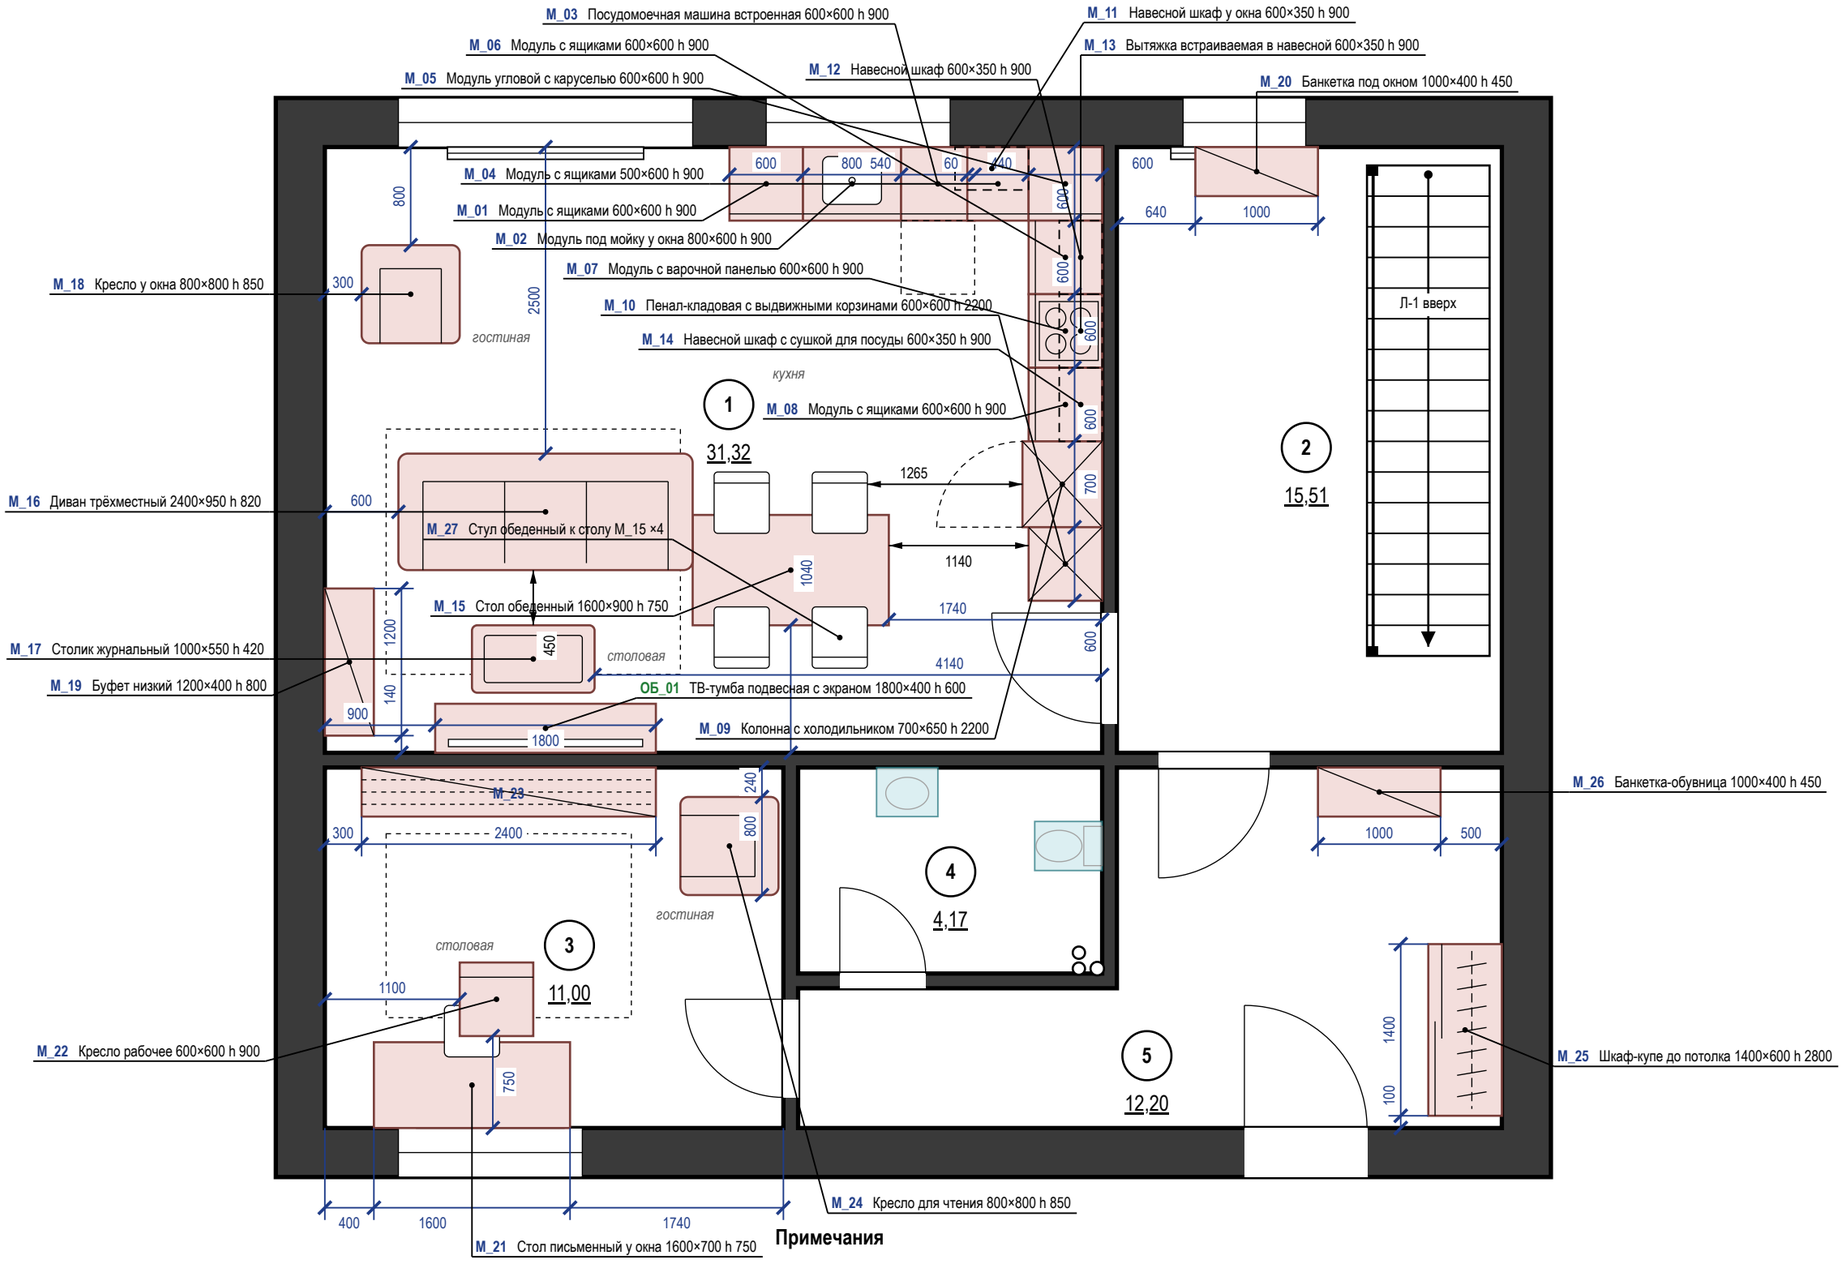

Экспликация помещений

лист обмерного плана · на плане — номера в марках

Ведомость мебели и оборудования

Марка	Наименование	Ш×Г×В, мм	Пом.	Кол.
M_01	Модуль с ящиками	600×600×900	1	1
M_02	Модуль под мойку у окна	800×600×900	1	1
M_03	Посудомоечная машина встроенная	600×600×900	1	1
M_04	Модуль с ящиками	500×600×900	1	1
M_05	Модуль угловой с каруселью	600×600×900	1	1
M_06	Модуль с ящиками	600×600×900	1	1
M_07	Модуль с варочной панелью	600×600×900	1	1
M_08	Модуль с ящиками	600×600×900	1	1
M_09	Колонна с холодильником	700×650×2200	1	1
M_10	Пенал-кладовая с выдвижными корзинами	600×600×2200	1	1
M_11	Навесной шкаф у окна	600×350×900	1	1
M_12	Навесной шкаф	600×350×900	1	1
M_13	Вытяжка встраиваемая в навесной	600×350×900	1	1
M_14	Навесной шкаф с сушкой для посуды	600×350×900	1	1
M_15	Стол обеденный 1600×900	1600×900×750	1	1
ОБ_01	ТВ-тумба подвесная с экраном	1800×400×600	1	1
M_16	Диван трёхместный	2400×950×820	1	1
M_17	Столик журнальный	1000×550×420	1	1
M_18	Кресло у окна	800×800×850	1	1
M_19	Буфет низкий	1200×400×800	1	1
M_20	Банкетка под окном	1000×400×450	2	1
M_21	Стол письменный у окна	1600×700×750	3	1
M_22	Кресло рабочее	600×600×900	3	1
M_23	Стеллаж для книг во всю стену	2400×400×2400	3	1
M_24	Кресло для чтения	800×800×850	3	1
M_25	Шкаф-купе до потолка	1400×600×2800	5	1
M_26	Банкетка-обувница	1000×400×450	5	1
M_27	Стул обеденный к столу M_15	450×500×820	1	4

Ш — вдоль стены (изголовья), Г — от стены (длина кровати)

Материалы, модели, допуск замены — лист 17


Примечания

1. Размеры — в мм от чистовых поверхностей стен; размеры мебели уточнить после отделочных работ; общие указания — лист 2.
2. Отступ от стены, на плане не образмерен: M_24 — 40 мм.
3. Стулья обеденной группы (M_27 — 4 шт.) показаны в рабочем положении, задвинутыми под столешницу на 150 мм.

					Проект: Дом 120 м²
	Лист	№ док.	Подпись	Дата	План размещения мебели и оборудования · 1-й этаж
Дизайнер	Кырлан А.С.			19.10.26	

Стадия	Лист	Листов
П	15	128

выпуск 19.10.2026 № 66b2a77b4d · стр. 15 из 128

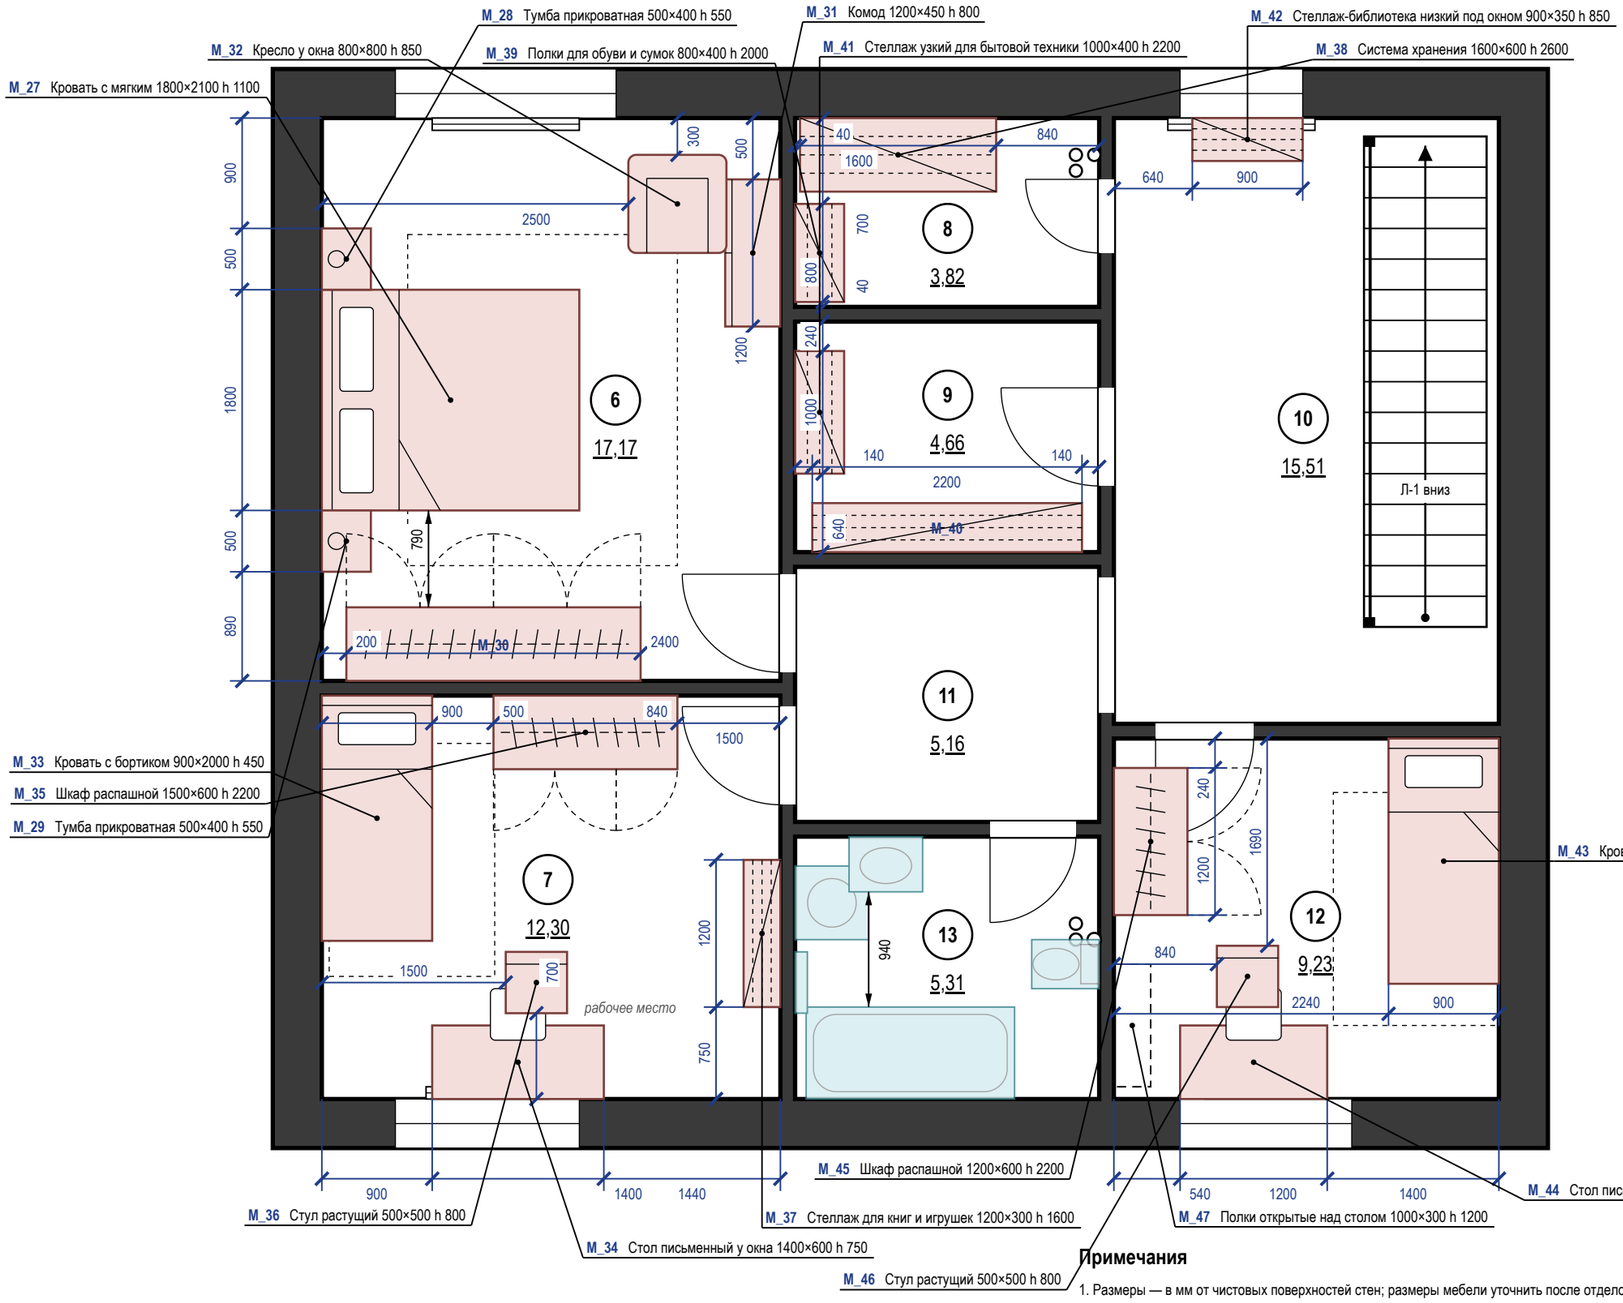

Экспликация помещений

лист обмерного плана · на плане — номера в марках

Ведомость мебели и оборудования

Марка	Наименование	Ш×Г×В, мм	Пом.	Кол.
M_27	Кровать 1800×2000 с мягким	1800×2100×1100	6	1
M_28	Тумба прикроватная	500×400×550	6	1
M_29	Тумба прикроватная	500×400×550	6	1
M_30	Шкаф распашной до потолка	2400×600×2600	6	1
M_31	Комод	1200×450×800	6	1
M_32	Кресло у окна	800×800×850	6	1
M_33	Кровать 900×2000 с бортиком	900×2000×450	7	1
M_34	Стол письменный у окна	1400×600×750	7	1
M_35	Шкаф распашной	1500×600×2200	7	1
M_36	Стул растущий	500×500×800	7	1
M_37	Стеллаж для книг и игрушек	1200×300×1600	7	1
M_38	Система хранения	1600×600×2600	8	1
M_39	Полки для обуви и сумок	800×400×2000	8	1
M_40	Стеллаж для хранения	2200×400×2200	9	1
M_41	Стеллаж узкий для бытовой техники	1000×400×2200	9	1
M_42	Стеллаж-библиотека низкий под окном	900×350×850	10	1
M_43	Кровать 900×2000 с бортиком	900×2000×450	12	1
M_44	Стол письменный у окна	1200×600×750	12	1
M_45	Шкаф распашной	1200×600×2200	12	1
M_46	Стул растущий	500×500×800	12	1
M_47	Полки открытые над столом	1000×300×1200	12	1

Ш — вдоль стены (изголовья), Г — от стены (длина кровати)

Материалы, модели, допуск замены — лист 17

Примечания

1. Размеры — в мм от чистовых поверхностей стен; размеры мебели уточнить после отделочных работ; общие указания — лист 2.

					Проект: Дом 120 м²
	Лист	№ док.	Подпись	Дата	План размещения мебели и оборудования · 2-й этаж
Дизайнер	Кырлан А.С.			19.10.26	

Стадия	Лист	Листов
П	16	128

выпуск 19.10.2026 № 66b2a77b4d · стр. 16 из 128

Поз.	Наименование и техническая характеристика	Тип, марка, обозначение документа, опросного листа	Код продукции	Поставщик	Ед. измерения	Кол.	Масса 1 ед., кг	Примечание
	Мебель встроенная и корпусная (изготовление по чертежам мебельщика)							
M_01	Модуль с ящиками; корпус ЛДСП, фасады — матовая эмаль в тон стен; Ш×Г×В 600×600×900 мм			изготовление на заказ	шт.	1		пом. 1
M_02	Модуль под мойку у окна; корпус ЛДСП, фасады — матовая эмаль в тон стен; Ш×Г×В 800×600×900 мм			изготовление на заказ	шт.	1		пом. 1
M_03	Посудомоечная машина встроенная; корпус ЛДСП, фасады — матовая эмаль в тон стен; Ш×Г×В 600×600×900 мм			изготовление на заказ	шт.	1		пом. 1
M_04	Модуль с ящиками; корпус ЛДСП, фасады — матовая эмаль в тон стен; Ш×Г×В 500×600×900 мм			изготовление на заказ	шт.	1		пом. 1
M_05	Модуль угловой с каруселью; корпус ЛДСП, фасады — матовая эмаль в тон стен; Ш×Г×В 600×600×900 мм			изготовление на заказ	шт.	1		пом. 1
M_06	Модуль с ящиками; корпус ЛДСП, фасады — матовая эмаль в тон стен; Ш×Г×В 600×600×900 мм			изготовление на заказ	шт.	1		пом. 1
M_07	Модуль с варочной панелью и духовым шкафом; корпус ЛДСП, фасады — матовая эмаль в тон стен; Ш×Г×В 600×600×900 мм			изготовление на заказ	шт.	1		пом. 1
M_08	Модуль с ящиками; корпус ЛДСП, фасады — матовая эмаль в тон стен; Ш×Г×В 600×600×900 мм			изготовление на заказ	шт.	1		пом. 1
M_09	Колонна с холодильником; корпус ЛДСП, фасады — матовая эмаль в тон стен; Ш×Г×В 700×650×2200 мм			изготовление на заказ	шт.	1		пом. 1
M_10	Пенал-кладовая с выдвижными корзинами; корпус ЛДСП, фасады — матовая эмаль в тон стен; Ш×Г×В 600×600×2200 мм			изготовление на заказ	шт.	1		пом. 1
M_11	Навесной шкаф у окна, витрина со стеклом; корпус ЛДСП, фасады — матовая эмаль в тон стен; Ш×Г×В 600×350×900 мм			изготовление на заказ	шт.	1		пом. 1
M_12	Навесной шкаф, фасад в тон цоколя; корпус ЛДСП, фасады — матовая эмаль в тон стен; Ш×Г×В 600×350×900 мм			изготовление на заказ	шт.	1		пом. 1
M_13	Вытяжка встраиваемая в навесной шкаф; корпус ЛДСП, фасады — матовая эмаль в тон стен; Ш×Г×В 600×350×900 мм			изготовление на заказ	шт.	1		пом. 1
M_14	Навесной шкаф с сушкой для посуды; корпус ЛДСП, фасады — матовая эмаль в тон стен; Ш×Г×В 600×350×900 мм			изготовление на заказ	шт.	1		пом. 1
M_25	Шкаф-купе до потолка, дуб табак; корпус ЛДСП, фасады — матовая эмаль в цвет стен (Tikkurila G503); Ш×Г×В 1400×600×2800 мм			изготовление на заказ	шт.	1		пом. 5
M_30	Шкаф распашной до потолка, фасады матовые; корпус ЛДСП, фасады — матовая эмаль в цвет стен (Tikkurila G503); Ш×Г×В 2400×600×2600 мм			изготовление на заказ	шт.	1		пом. 6
M_35	Шкаф распашной; корпус ЛДСП, фасады — матовая эмаль в цвет стен (Tikkurila G503); Ш×Г×В 1500×600×2200 мм			изготовление на заказ	шт.	1		пом. 7
M_38	Система хранения: штанги, полки, ящики; каркас и полки — ЛДСП, декор «дуб натуральный»; Ш×Г×В 1600×600×2600 мм			изготовление на заказ	шт.	1		пом. 8; крепление к стене
M_39	Полки для обуви и сумок; каркас и полки — ЛДСП, декор «дуб натуральный»; Ш×Г×В 800×400×2000 мм			изготовление на заказ	шт.	1		пом. 8; крепление к стене
M_45	Шкаф распашной; корпус ЛДСП, фасады — матовая эмаль в цвет стен (Tikkurila G503); Ш×Г×В 1200×600×2200 мм			изготовление на заказ	шт.	1		пом. 12
	Мебель покупная							
M_15	Стол обеденный 1600×900, дуб табак; шпон, дуб натуральный, матовое масло; Ш×Г×В 1600×900×750 мм			аналог по характеристикам	шт.	1		пом. 1; замена ≤ габарита
M_16	Диван трёхместный, лён; обивка — ткань, цвет NCS S 1010-Y20R; Ш×Г×В 2400×950×820 мм			аналог по характеристикам	шт.	1		пом. 1; замена ≤ габарита
M_17	Столик журнальный, дуб и латунь; шпон, дуб натуральный, матовое масло; Ш×Г×В 1000×550×420 мм			аналог по характеристикам	шт.	1		пом. 1; замена ≤ габарита
M_18	Кресло у окна, букле; обивка — ткань, цвет NCS S 1010-Y20R; Ш×Г×В 800×800×850 мм			аналог по характеристикам	шт.	1		пом. 1; замена ≤ габарита
M_19	Буфет низкий, дуб табак; шпон, дуб натуральный, матовое масло; Ш×Г×В 1200×400×800 мм			аналог по характеристикам	шт.	1		пом. 1; крепление к стене; замена ≤ габарита
M_48	Стул обеденный к столу M_15; обивка — ткань, цвет NCS S 1010-Y20R; каркас — дуб натуральный; Ш×Г×В 450×500×820 мм			аналог по характеристикам	шт.	4		пом. 1; замена ≤ габарита
ОБ_01	ТВ-тумба подвесная с экраном, дуб табак; шпон, дуб натуральный, матовое масло; Ш×Г×В 1800×400×600 мм			аналог по характеристикам	шт.	1		пом. 1; замена ≤ габарита
M_20	Банкетка под окном, дуб табак; Ш×Г×В 1000×400×450 мм			аналог по характеристикам	шт.	1		пом. 2; замена ≤ габарита
M_21	Стол письменный у окна, дуб табак; шпон, дуб натуральный, матовое масло; Ш×Г×В 1600×700×750 мм			аналог по характеристикам	шт.	1		пом. 3; замена ≤ габарита
M_22	Кресло рабочее; обивка — ткань, цвет NCS S 1010-Y20R; каркас — дуб натуральный; Ш×Г×В 600×600×900 мм			аналог по характеристикам	шт.	1		пом. 3; замена ≤ габарита
M_23	Стеллаж для книг во всю стену; шпон, дуб натуральный, матовое масло; Ш×Г×В 2400×400×2400 мм			аналог по характеристикам	шт.	1		пом. 3; крепление к стене; замена ≤ габарита
M_24	Кресло для чтения; обивка — ткань, цвет NCS S 1010-Y20R; Ш×Г×В 800×800×850 мм			аналог по характеристикам	шт.	1		пом. 3; замена ≤ габарита
M_26	Банкетка-обувница; Ш×Г×В 1000×400×450 мм			аналог по характеристикам	шт.	1		пом. 5; замена ≤ габарита
M_27	Кровать 1800×2000 с мягким изголовьем 1100, лён; мягкое изголовье, обивка — ткань, цвет NCS S 1010-Y20R; Ш×Г×В 1800×2100×1100 мм			аналог по характеристикам	шт.	1		пом. 6; замена ≤ габарита

Примечания

1. Позиции мебели совпадают с марками на плане расстановки; размеры Ш×Г×В — Ш вдоль стены, Г от стены.
2. Встроенная и корпусная мебель изготавливается по чертежам мебельщика после контрольного обмера; графы «Тип, марка» и «Код продукции» для неё не заполняются (ГОСТ 21.110-2013).
3. Покупные изделия — аналог по характеристикам: заменять только на изделия не больше указанного габарита и того же материала и цвета.
4. Материал и цвет, не указанные в данных изделия, приняты по концепции: тон дерева — по полу, обивка — по вторичному цвету палитры; образцы согласовать до заказа.
5. Масса 1 ед. для изделий до 25 кг не указывается. Техника — по монтажным схемам изготовителя; выводы — по листам ЭОМ и ВК.

					Проект: Дом 120 м²
	Лист	№ док.	Подпись	Дата	Спецификация мебели и оборудования
Дизайнер	Кырлан А.С.			19.10.26	

Стадия	Лист	Листов
П	17	128

выпуск 19.10.2026 № 66b2a77b4d · стр. 17 из 128

Поз.	Наименование и техническая характеристика	Тип, марка, обозначение документа, опросного листа	Код продукции	Поставщик	Ед. измерения	Кол.	Масса 1 ед., кг	Примечание
M_28, M_29	Тумба прикроватная, дуб табак; шпон, дуб натуральный, матовое масло; Ш×Г×В 500×400×550 мм			аналог по характеристикам	шт.	2		пом. 6; замена ≤ габарита
M_31	Комод, дуб табак; шпон, дуб натуральный, матовое масло; Ш×Г×В 1200×450×800 мм			аналог по характеристикам	шт.	1		пом. 6; крепление к стене; замена ≤ габарита
M_32	Кресло у окна; обивка — ткань, цвет NCS S 1010-Y20R; Ш×Г×В 800×800×850 мм			аналог по характеристикам	шт.	1		пом. 6; замена ≤ габарита
M_33, M_43	Кровать 900×2000 с бортиком; мягкое изголовье, обивка — ткань, цвет NCS S 1010-Y20R; Ш×Г×В 900×2000×450 мм			аналог по характеристикам	шт.	2		пом. 7, 12; замена ≤ габарита
M_34	Стол письменный у окна; шпон, дуб натуральный, матовое масло; Ш×Г×В 1400×600×750 мм			аналог по характеристикам	шт.	1		пом. 7; замена ≤ габарита
M_36, M_46	Стул растущий; обивка — ткань, цвет NCS S 1010-Y20R; каркас — дуб натуральный; Ш×Г×В 500×500×800 мм			аналог по характеристикам	шт.	2		пом. 7, 12; замена ≤ габарита
M_37	Стеллаж для книг и игрушек; шпон, дуб натуральный, матовое масло; Ш×Г×В 1200×300×1600 мм			аналог по характеристикам	шт.	1		пом. 7; крепление к стене; замена ≤ габарита
M_40	Стеллаж для хранения; каркас и полки — ЛДСП, декор «дуб натуральный»; Ш×Г×В 2200×400×2200 мм			аналог по характеристикам	шт.	1		пом. 9; крепление к стене; замена ≤ габарита
M_41	Стеллаж узкий для бытовой техники; каркас и полки — ЛДСП, декор «дуб натуральный»; Ш×Г×В 1000×400×2200 мм			аналог по характеристикам	шт.	1		пом. 9; крепление к стене; замена ≤ габарита
M_42	Стеллаж-библиотека низкий под окном; шпон, дуб натуральный, матовое масло; Ш×Г×В 900×350×850 мм			аналог по характеристикам	шт.	1		пом. 10; крепление к стене; замена ≤ габарита
M_44	Стол письменный у окна; шпон, дуб натуральный, матовое масло; Ш×Г×В 1200×600×750 мм			аналог по характеристикам	шт.	1		пом. 12; замена ≤ габарита
M_47	Полки открытые над столом; каркас и полки — ЛДСП, декор «дуб натуральный»; Ш×Г×В 1000×300×1200 мм			аналог по характеристикам	шт.	1		пом. 12; крепление к стене; замена ≤ габарита
	Техника встраиваемая и бытовая, светильники под розетки							
	Посудомоечная машина встраиваемая, в модуле M_03; ниша 600 мм			аналог по характеристикам	шт.	1		пом. 1; по схеме изготовителя
	Варочная панель встраиваемая, электрическая, в модуле M_07			аналог по характеристикам	шт.	1		пом. 1; по схеме изготовителя
	Духовой шкаф встраиваемый, в модуле M_07			аналог по характеристикам	шт.	1		пом. 1; по схеме изготовителя
	Холодильник встраиваемый, в модуле M_09			аналог по характеристикам	шт.	1		пом. 1; по схеме изготовителя
	Вытяжка встраиваемая, в модуле M_13			аналог по характеристикам	шт.	1		пом. 1; по схеме изготовителя
	Стиральная машина, место по листу ВК (ОБ_02); Ш×Г 600×600 мм			аналог по характеристикам	шт.	1		пом. 13; по схеме изгото́вителя
	Торшер, у поз. M_18; абажур — ткань или опаловое стекло; лампа 2700 K			аналог по характеристикам	шт.	1		пом. 1; розетка P21 (ЭОМ)
	Торшер, у поз. M_32; абажур — ткань или опаловое стекло; лампа 2700 K			аналог по характеристикам	шт.	1		пом. 6; розетка P5 (ЭОМ)
	Текстиль							
T13	Портьеры-волна (гостиная); лён 70 %, вискоза 30 %; цвет NCS S 1010-Y20R; карниз 3000 мм, высота 2870 мм, сборка 2			аналог по характеристикам	шт.	2		пом. 1
T14	Тюль (гостиная); полиэстер 100 %; цвет Little Greene No. 222; карниз 3000 мм, высота 2870 мм, сборка 2,5			аналог по характеристикам	шт.	1		пом. 1
T15	Римская штора (кухня); лён 100 %; цвет Tikkurila X463; карниз 1500 мм, высота 1600 мм			аналог по характеристикам	шт.	1		пом. 1
T16	Ковёр в зоне отдыха; шерсть 100 %; цвет Tikkurila X463; 2400×2000 мм			аналог по характеристикам	шт.	1		пом. 1; с подложкой
T17	Подушки на диван; букле (шерсть 60 %, полиэстер 40 %); цвет NCS S 1010-Y20R			аналог по характеристикам	шт.	3		пом. 1
T18	Подушки на диван, акцент; хлопковый бархат 100 %; цвет NCS S 3050-R80B			аналог по характеристикам	шт.	2		пом. 1
T19	Плед на диван; альпака 50 %, шерсть 50 %; цвет Tikkurila X463			аналог по характеристикам	шт.	1		пом. 1
T7	Портьеры-волна; лён 100 %; цвет NCS S 1010-Y20R; карниз 2100 мм, высота 2870 мм, сборка 2			аналог по характеристикам	шт.	2		пом. 3
T8	Тюль; полиэстер 100 %; цвет Little Greene No. 222; карниз 2100 мм, высота 2870 мм, сборка 2,5			аналог по характеристикам	шт.	1		пом. 3
T9	Ковёр под кроватью; шерсть 100 %; цвет Tikkurila X463; 2000×1500 мм			аналог по характеристикам	шт.	1		пом. 3; с подложкой
T10	Подушки декоративные на кровать; букле (шерсть 60 %, полиэстер 40 %); цвет NCS S 1010-Y20R			аналог по характеристикам	шт.	3		пом. 3
T11	Подушки на кровать, акцент; хлопковый бархат 100 %; цвет NCS S 5020-G90Y			аналог по характеристикам	шт.	2		пом. 3
T12	Плед на кровать; шерсть мериноса 100 %; цвет NCS S 5020-G90Y			аналог по характеристикам	шт.	1		пом. 3

					Проект: Дом 120 м²
	Лист	№ док.	Подпись	Дата	Спецификация мебели и оборудования (продолжение)
Дизайнер	Кырлан А.С.			19.10.26	

Стадия	Лист	Листов
П	18	128

выпуск 19.10.2026 № 66b2a77b4d · стр. 18 из 128

Поз.	Наименование и техническая характеристика	Тип, марка, обозначение документа, опросного листа	Код продукции	Поставщик	Ед. измерения	Кол.	Масса 1 ед., кг	Примечание
Т1	Портьеры-волна; лён 100 %; цвет NCS S 1010-Y20R; карниз 2400 мм, высота 2870 мм, сборка 2			аналог по характеристикам	шт.	2		пом. 6
Т2	Тюль; полиэстер 100 %; цвет Little Greene No. 222; карниз 2400 мм, высота 2870 мм, сборка 2,5			аналог по характеристикам	шт.	1		пом. 6
Т3	Ковёр под кроватью; шерсть 80 %, хлопок 20 %; цвет Tikkurila X395; 2200×2700 мм			аналог по характеристикам	шт.	1		пом. 6; с подложкой
Т4	Подушки декоративные на кровать; лён 100 %; цвет NCS S 1010-Y20R			аналог по характеристикам	шт.	3		пом. 6
Т5	Подушки на кровать, акцент; хлопковый бархат 100 %; цвет Farrow & Ball No. 89			аналог по характеристикам	шт.	2		пом. 6
Т6	Плед на кровать; шерсть мериноса 100 %; цвет Farrow & Ball No. 89			аналог по характеристикам	шт.	1		пом. 6
Т20	Портьеры-волна; лён 100 %; цвет NCS S 1010-Y20R; карниз 2100 мм, высота 2870 мм, сборка 2			аналог по характеристикам	шт.	2		пом. 7
Т21	Тюль; полиэстер 100 %; цвет Little Greene No. 222; карниз 2100 мм, высота 2870 мм, сборка 2,5			аналог по характеристикам	шт.	1		пом. 7
Т22	Ковёр под кроватью; шерсть 100 %; цвет Tikkurila X463; 1350×1900 мм			аналог по характеристикам	шт.	1		пом. 7; с подложкой
Т23	Подушки декоративные на кровать; букле (шерсть 60 %, полиэстер 40 %); цвет NCS S 1010-Y20R			аналог по характеристикам	шт.	3		пом. 7
Т24	Подушки на кровать, акцент; хлопковый бархат 100 %; цвет Farrow & Ball No. 66			аналог по характеристикам	шт.	2		пом. 7
Т25	Плед на кровать; шерсть мериноса 100 %; цвет Farrow & Ball No. 66			аналог по характеристикам	шт.	1		пом. 7
Т26	Портьеры-волна; лён 100 %; цвет NCS S 1010-Y20R; карниз 2000 мм, высота 2870 мм, сборка 2			аналог по характеристикам	шт.	2		пом. 12
Т27	Тюль; полиэстер 100 %; цвет Little Greene No. 222; карниз 2000 мм, высота 2870 мм, сборка 2,5			аналог по характеристикам	шт.	1		пом. 12
Т28	Ковёр под кроватью; шерсть 100 %; цвет Tikkurila X463; 1350×1900 мм			аналог по характеристикам	шт.	1		пом. 12; с подложкой
Т29	Подушки декоративные на кровать; букле (шерсть 60 %, полиэстер 40 %); цвет NCS S 1010-Y20R			аналог по характеристикам	шт.	3		пом. 12
Т30	Подушки на кровать, акцент; хлопковый бархат 100 %; цвет Tikkurila H440			аналог по характеристикам	шт.	2		пом. 12
Т31	Плед на кровать; шерсть мериноса 100 %; цвет Tikkurila H440			аналог по характеристикам	шт.	1		пом. 12
	Декор							
ДК6	Картина над креслом: пейзаж, масло, рама — дуб табак; 1000×800 мм; центр на 1550 мм от пола			аналог по характеристикам	шт.	1	6	пом. 1; крепление: анкер, 2 шт.
ДК7	Растение в кашпо; 450×450 мм			аналог по характеристикам	шт.	1		пом. 1
ДК8	Ваза керамическая с ветками на обеденном столе; 200×350 мм; на M_15			аналог по характеристикам	шт.	1		пом. 1
ДК40	Олива в кадке Ø450 у окна; 450×450 мм			аналог по характеристикам	шт.	1		пом. 1
ДК41	Сансевиерия в кашпо Ø400 под лестницей; 400×400 мм			аналог по характеристикам	шт.	1		пом. 2
ДК3	Картина над креслом: гравюра в паспарту, рама — графит; 550×450 мм; низ на 1050 мм от пола			аналог по характеристикам	шт.	1	4	пом. 3; крепление к стене
ДК9	Зеркало над умывальником, влагостойкое; 500×700 мм; низ на 1100 мм от пола			аналог по характеристикам	шт.	1	4	пом. 4; крепление к стене
ДК5	Зеркало; рама — чёрный матовый; 600×1800 мм; низ на 550 мм от пола			аналог по характеристикам	шт.	1	18	пом. 5; крепление: анкер, 4 шт.
ДК43	Замиокулькас в кашпо Ø350; 350×350 мм			аналог по характеристикам	шт.	1		пом. 5
ДК1	Картина над кроватью: акварель, рама — светлый дуб; 1000×700 мм; низ на 1300 мм от пола			аналог по характеристикам	шт.	1	4	пом. 6; крепление к стене
ДК44	Аглаонема в кашпо Ø400; 400×400 мм			аналог по характеристикам	шт.	1		пом. 6
ДК2	Картина над кроватью: детская иллюстрация, рама — белёный дуб; 600×450 мм; низ на 650 мм от пола			аналог по характеристикам	шт.	1	4	пом. 7; крепление к стене
ДК4	Зеркало в рост в тонкой чёрной раме; рама — чёрный матовый; 500×1600 мм; низ на 300 мм от пола			аналог по характеристикам	шт.	1	12	пом. 7; крепление: анкер для пустотелых оснований, 4 шт.
ДК45	Хлорофитум в кашпо Ø350 у окна; 350×350 мм			аналог по характеристикам	шт.	1		пом. 10
ДК46	Сансевиерия в кашпо Ø400; 400×400 мм			аналог по характеристикам	шт.	1		пом. 11
ДК10	Картина над кроватью: детский принт, рама — светлый ясень; 600×450 мм; низ на 650 мм от пола			аналог по характеристикам	шт.	1	4	пом. 12; крепление к стене
ДК11	Зеркало в рост в тонкой чёрной раме; рама — чёрный матовый; 500×1600 мм; низ на 300 мм от пола			аналог по характеристикам	шт.	1	12	пом. 12; крепление: анкер для пустотелых оснований, 4 шт.
ДК12	Зеркало над умывальником, влагостойкое; 600×750 мм; низ на 1100 мм от пола			аналог по характеристикам	шт.	1	4	пом. 13; крепление к стене

	Лист	№ док.	Подпись	Дата
Дизайнер	Кырлан А.С.			19.10.26

Проект: Дом 120 м²

Спецификация мебели и оборудования (продолжение)

Стадия	Лист	Листов
П	19	128

Ведомость изделий

Марка	Наименование	Пом.	Ш×Г×В, мм	Корпус	Фасад	Кромка, мм скр./вид.	Кол.
M_25	Шкаф-купе	5	1400×600×2800	ЛДСП 16	рифлёные панели МДФ в алюминиевом профиле	0,4 / 2	1
M_30	Шкаф распашной	6	2400×600×2600	ЛДСП 16	МДФ 18, эмаль матовая	0,4 / 2	1
M_35	Шкаф распашной	7	1500×600×2200	ЛДСП 16	МДФ 18, эмаль матовая	0,4 / 2	1
M_38	Система хранения	8	1600×600×2600	ЛДСП 16	без фасадов; ящики — МДФ 18, эмаль матовая	0,4 / 2	1
M_39	Система хранения	8	800×400×2000	ЛДСП 16	без фасадов; ящики — МДФ 18, эмаль матовая	0,4 / 2	1
M_40	Система хранения	9	2200×400×2200	ЛДСП 16	без фасадов; ящики — МДФ 18, эмаль матовая	0,4 / 2	1
M_41	Система хранения	9	1000×400×2200	ЛДСП 16	без фасадов; ящики — МДФ 18, эмаль матовая	0,4 / 2	1
M_45	Шкаф распашной	12	1200×600×2200	ЛДСП 16	МДФ 18, эмаль матовая	0,4 / 2	1
M_47	Система хранения	12	1000×300×1200	ЛДСП 16	без фасадов; ящики — МДФ 18, эмаль матовая	0,4 / 2	1
M_01	Модуль нижний: ящики	1	600×600×900	ЛДСП 16	МДФ 18, эмаль матовая	0,4 / 2	1
M_02	Модуль нижний: мойка	1	800×600×900	ЛДСП 16	МДФ 18, эмаль матовая	0,4 / 2	1
M_03	Модуль нижний: ПММ	1	600×600×900	ЛДСП 16	МДФ 18, эмаль матовая	0,4 / 2	1
M_11	Модуль навесной: полки	1	600×350×900	ЛДСП 16	МДФ 18, эмаль матовая	0,4 / 2	1
M_04	Модуль нижний: ящики	1	500×600×900	ЛДСП 16	МДФ 18, эмаль матовая	0,4 / 2	1
M_05	Модуль нижний: ящики	1	600×600×900	ЛДСП 16	МДФ 18, эмаль матовая	0,4 / 2	1
M_06	Модуль нижний: ящики	1	600×600×900	ЛДСП 16	МДФ 18, эмаль матовая	0,4 / 2	1
M_12	Модуль навесной: полки	1	600×350×900	ЛДСП 16	МДФ 18, эмаль матовая	0,4 / 2	1
M_07	Модуль нижний: духовой шкаф, варочная	1	600×600×900	ЛДСП 16	МДФ 18, эмаль матовая	0,4 / 2	1
M_13	Модуль навесной: полки	1	600×350×900	ЛДСП 16	МДФ 18, эмаль матовая	0,4 / 2	1
M_08	Модуль нижний: ящики	1	600×600×900	ЛДСП 16	МДФ 18, эмаль матовая	0,4 / 2	1
M_14	Модуль навесной: полки	1	600×350×900	ЛДСП 16	МДФ 18, эмаль матовая	0,4 / 2	1
M_09	Пенал: холодильник встр.	1	700×650×2200	ЛДСП 16	МДФ 18, эмаль матовая	0,4 / 2	1
M_10	Пенал: полки	1	600×600×2200	ЛДСП 16	МДФ 18, эмаль матовая	0,4 / 2	1

Ведомость встраиваемой техники

Поз.	Прибор	Ниша, вырез, мм	Вентиляция	Питание	Схема
M_02	Мойка врезная / подстольная с сифоном	вырез по шаблону, ориентир 700 × 480		смеситель — выводы ВК	по модели
M_03	Посудомоечная машина встраиваемая, 60 см	ниша 600 × 862 (от пола до низа столешницы)	зазор в цоколе, по схеме	розетка в соседнем модуле	по модели
M_07	Духовой шкаф встраиваемый, 60 см	ниша 560 × 595, глубина ≥ 550	зазор за шкафом, вырез в задней стенке	вывод кабеля под шкафом	по модели
M_07	Варочная панель индукционная, 60 см	вырез в столешнице 560 × 490		вывод кабеля под модулем	по модели
M_09	Холодильник встраиваемый, ниша 1780	ниша 1780 × 560 × 550	решётка в цоколе, канал за корпусом, выход сверху	розетка над нишей или в соседнем модуле	по модели
M_07	Вытяжка настенная, 60 см	низ ≥ 650 над панелью	воздуховод к вентканалу, короб до потолка	вывод кабеля в коробе	по модели

Примечания

1. Модели техники выбирает заказчик до изготовления мебели; ниши, вырезы и вентиляция — по монтажной схеме выбранной модели (условие гарантии), её номер вносится в ведомость.
2. Количество фурнитуры — по чертежам изделий; запас крепежа 5 %. Аналоги — по характеристикам (доводчик, нагрузка, ход).
3. Цвет корпусов, фасадов и профилей — по колерной карте проекта.


Ведомость фурнитуры

№	Фурнитура	Тип, размер	Изделия	Кол.
1	Система дверей купе: профиль, направляющие, ролики	на 2 двери	M_25	1
2	Ручка-профиль вертикальная	в цвет профиля	M_25	2
3	Полкодержатель с фиксацией	ø5 мм	M_25, M_30, M_35, M_38, M_40, M_41, M_45, M_47, M_11, M_12, M_13, M_14, M_09, M_10	256
4	Штанга овальная 30×15, L = 676	+ 2 держателя	M_25	1
5	Полка для обуви выдвижная наклонная	ширина 676	M_25	3
6	Опора регулируемая с цоколем на клипсах	ход 20 мм	M_25, M_30, M_35, M_38, M_39, M_40, M_41, M_45	50
7	Анкер по основанию стены	по таблице крепежа	M_25, M_30, M_35, M_38, M_39, M_40, M_41, M_45, M_47, M_11, M_12, M_13, M_14	64
8	Уголок крепления к стене от опрокидывания	стальной	M_25, M_30, M_35, M_38, M_39, M_40, M_41, M_45, M_47, M_09, M_10	22
9	Петля накладная 110° с доводчиком	чашка 35 мм	M_30, M_35, M_45, M_02, M_11, M_12, M_13, M_14, M_09, M_10	98
10	Штанга овальная 30×15, L = 936	+ 2 держателя	M_30	2
11	Штанга овальная 30×15, L = 456	+ 2 держателя	M_30	1
12	Штанга овальная 30×15, L = 976	+ 2 держателя	M_35	1
13	Штанга овальная 30×15, L = 776	+ 2 держателя	M_38, M_45	2
14	Штанга выдвижная торцевая	L по глубине	M_39, M_40, M_41	5
15	Направляющие полного выдвижения с доводчиком NL 500	пара	M_01, M_04, M_05, M_06, M_07, M_08	16
16	Ручка-профиль	латунь матовая	M_01, M_02, M_03, M_11, M_04, M_05, M_06, M_12, M_07, M_13, M_08, M_14, M_09, M_10	32
17	Опора кухонная регулируемая 100–120 мм	+ клипса цоколя	M_01, M_02, M_03, M_04, M_05, M_06, M_07, M_08, M_09, M_10	44
18	Комплект навески фасада ПММ	из поставки машины	M_03	1
19	Навес регулируемый для навесного шкафа	пара на секцию	M_11, M_12, M_13, M_14	4
20	Шина монтажная	L = 540	M_11, M_12, M_13, M_14	4


					Проект: Дом 120 м²			
	Лист	№ док.	Подпись	Дата	Ведомости изделий, техники и фурнитуры	Стадия	Лист	Листов
Дизайнер	Кырлан А.С.			19.10.26		П	20	128

выпуск 19.10.2026 № 66b2a77b4d · стр. 20 из 128

Фрагмент 1. Санузел гостевой (пом. 4)

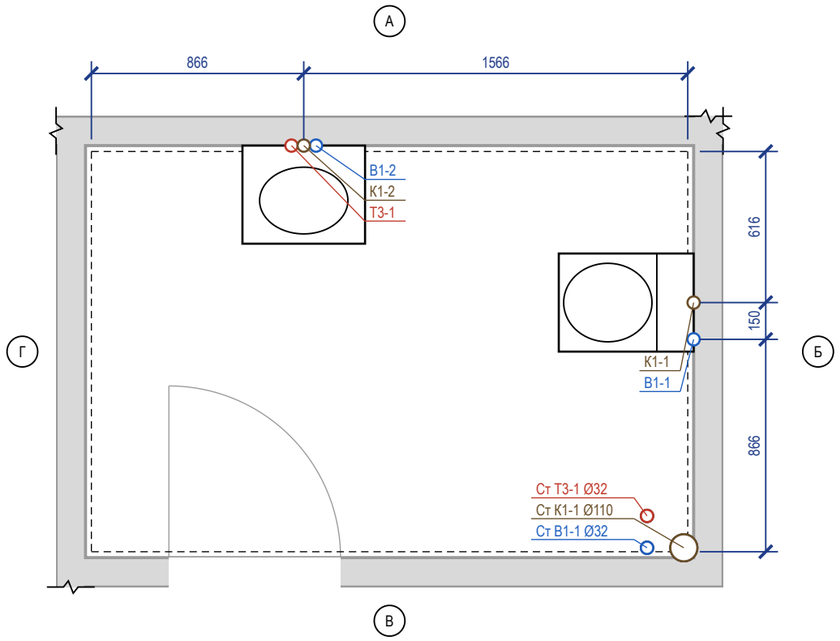

Фрагмент 2. Гостиная-кухня (пом. 1)

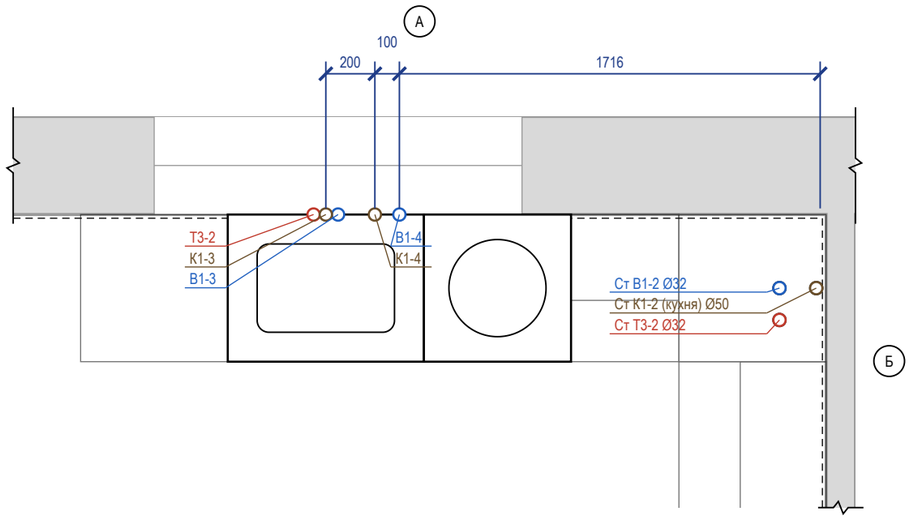

Ведомость привязок выводов

Код	Прибор	Ø	H, мм	Привязка от чист. стен, мм	Прим.
В1-1	С_01 унитаз подвесной	½"	250	ст. Б: 766 от А	в раме инсталляции
К1-1	С_01 унитаз подвесной	Ø110	220	ст. Б: 616 от А	
В1-2	С_02 умывальник	½"	600	ст. А: 916 от Г	межос. 100
Т3-1	С_02 умывальник	½"	600	ст. А: 816 от Г	межос. 100
К1-2	С_02 умывальник	Ø50	500	ст. А: 866 от Г	
В1-3	П3 мойка кухонная	½"	600	ст. А: 1966 от Б	межос. 100
Т3-2	П3 мойка кухонная	½"	600	ст. А: 2066 от Б	межос. 100
К1-3	П3 мойка кухонная	Ø50	400	ст. А: 2016 от Б	
В1-4	П4 посудомоечная машина	½"	550	ст. А: 1716 от Б	кран ПММ в шкафу мойки
К1-4	П4 посудомоечная машина	Ø40	550	ст. А: 1816 от Б	слив ПММ в шкафу мойки

Условные обозначения

- вывод В1 (код — в ведомости привязок)
- вывод Т3 (код — в ведомости привязок)
- вывод К1 (код — в ведомости привязок)
- сантехприбор по расстановке (габарит модели)
- чистовая поверхность стены (от неё привязки)
- стояк «Ст К1-N / Ст В1-N» (ГОСТ 21.601), Ø мм
- линия обрыва (граница фрагмента)
- А — обозначение стены А–Г (как на развёртках)

Примечания


1. Привязки выводов даны от чистовых поверхностей стен (облицовка на сторону: санузел гостевой — 24 мм (штукатурка 10 + клей 5 + плитка 9); гостиная-кухня — 24 мм (фартук: штукатурка 10 + клей 5 + плитка 9)); эти же грани — на развёртках и в раскладке плитки. Высоты — от чистого пола помещения.
2. До черновой разводки сверить по паспорту выбранного прибора (смеситель, инсталляция, сифон).
3. Горячая вода (Т3) — слева от холодной (В1), если смотреть на прибор. Допуск установки выводов: ±5 мм в группе, ±20 мм у отдельно стоящих.
4. Расчёт систем водоснабжения и канализации и подбор оборудования выполняет проектная организация; лист задаёт места и высоты выводов.
5. Посудомоечная машина П4: кран и слив — отдельными выводами в шкафу мойки (не за машиной), до машины ≤ 1500 мм.
6. Прибор П3 мойка кухонная, П4 посудомоечная машина взят из расстановки мебели (по шкафу с мойкой).
7. Стояки в коробах/шахтах не замоноличивать; стояк К1 в коробе — звукоизоляция стояка в коробе без жёсткого контакта с трубой; к арматуре и ревизиям — люк не меньше 300×400.

					Проект: Дом 120 м²
	Лист	№ док.	Подпись	Дата	План выводов сантехники · 1-й этаж
Дизайнер	Кырлан А.С.			19.10.26	

Стадия	Лист	Листов
П	21	128

выпуск 19.10.2026 № 66b2a77b4d · стр. 21 из 128

Фрагмент 1. Санузел второго этажа (пом. 13)

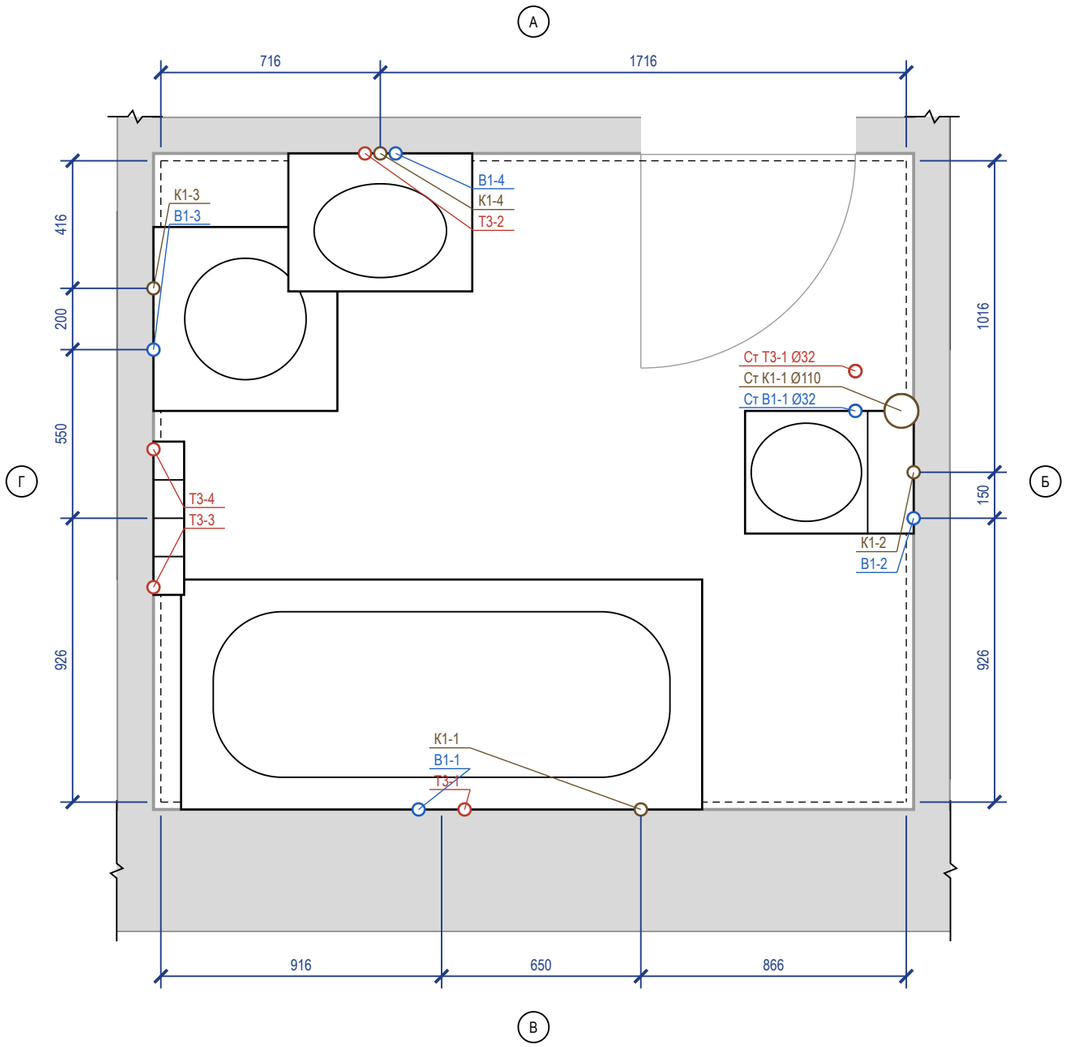

Ведомость привязок выводов

Код	Прибор	Ø	H, мм	Привязка от чист. стен, мм	Прим.
В1-1	С_03 ванна	½"	800	ст. В: 841 от Г	межос. 150
Т3-1	С_03 ванна	½"	800	ст. В: 991 от Г	межос. 150
К1-1	С_03 ванна	Ø50	50	ст. В: 866 от Б	
В1-2	С_04 унитаз подвесной	½"	250	ст. Б: 926 от В	в раме инсталляции
К1-2	С_04 унитаз подвесной	Ø110	220	ст. Б: 1016 от А	
В1-3	ОБ_02 стиральная машина	½"	600	ст. Г: 616 от А	кран машины
К1-3	ОБ_02 стиральная машина	Ø50	600	ст. Г: 416 от А	
В1-4	С_05 умывальник	½"	600	ст. А: 766 от Г	межос. 100
Т3-2	С_05 умывальник	½"	600	ст. А: 666 от Г	межос. 100
К1-4	С_05 умывальник	Ø50	500	ст. А: 716 от Г	
Т3-3	С_06 полотенцесушитель	½"	1150	ст. Г: 701 от В	подача, межос. 450; байпас и краны
Т3-4	С_06 полотенцесушитель	½"	1150	ст. Г: 941 от А	обратка

Условные обозначения

- вывод В1 (код — в ведомости привязок)
- вывод Т3 (код — в ведомости привязок)
- вывод К1 (код — в ведомости привязок)
- сантехприбор по расстановке (габарит модели)
- чистовая поверхность стены (от неё привязки)
- стояк «Ст К1-N / Ст В1-N» (ГОСТ 21.601), Ø мм
- линия обрыва (граница фрагмента)
- А — обозначение стены А–Г (как на развёртках)

Примечания


1. Привязки выводов даны от чистовых поверхностей стен (облицовка на сторону: санузел второго этажа — 24 мм (штукатурка 10 + клей 5 + плитка 9)); эти же грани — на развёртках и в раскладке плитки. Высоты — от чистого пола помещения.
2. До черновой разводки сверить по паспорту выбранного прибора (смеситель, инсталляция, сифон).
3. Горячая вода (Т3) — слева от холодной (В1), если смотреть на прибор. Допуск установки выводов: ±5 мм в группе, ±20 мм у отдельно стоящих.
4. Расчёт систем водоснабжения и канализации и подбор оборудования выполняет проектная организация; лист задаёт места и высоты выводов.
5. Стояки в коробах/шахтах не замоноличивать; стояк К1 в коробе — звукоизоляция стояка в коробе без жёсткого контакта с трубой; к арматуре и ревизиям — люк не меньше 300×400.

					Проект: Дом 120 м²
	Лист	№ док.	Подпись	Дата	План выводов сантехники · 2-й этаж
Дизайнер	Кырлан А.С.			19.10.26	


Стадия	Лист	Листов
П	22	128

выпуск 19.10.2026 № 66b2a77b4d · стр. 22 из 128


План квартиры (М 1:200)

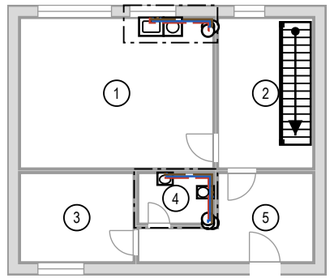

Фр. 1. Санузел гостевой (М 1:25)

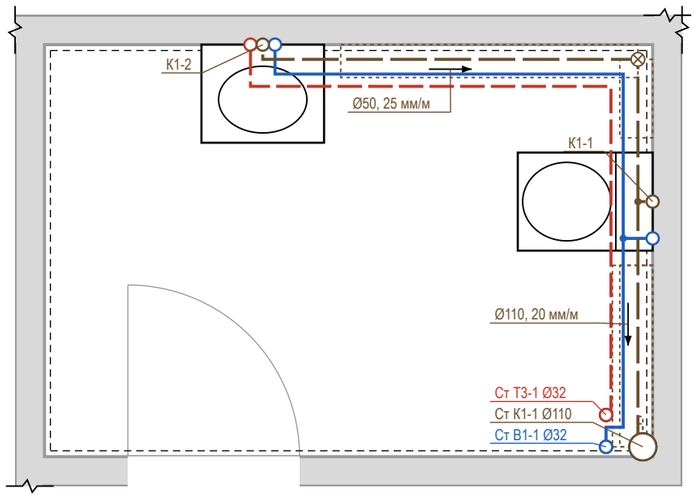

Фр. 2. Гостиная-кухня (М 1:25)

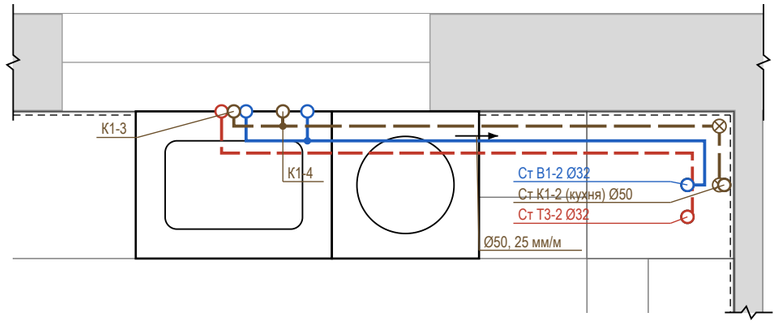

Условные обозначения


- В1 — водопровод хозяйственно-питьевой (ХВС), PP-R Ø20
- Т3 — горячее водоснабжение, подача (ГВС), PP-R Ø20
- К1 — канализация бытовая
- направление уклона К1 / пола: Ø, мм на 1 м
- ревизия (прочистка) К1 — доступ сохранить
- тройник (ответвление к прибору)
- короб К1 над чистым полом (ГКЛВ под плитку)
- вывод В1 (код — в ведомости привязок)
- вывод Т3 (код — в ведомости привязок)
- вывод К1 (код — в ведомости привязок)
- сантехприбор по расстановке (габарит модели)
- стояк «Ст К1-N / Ст В1-N» (ГОСТ 21.601), Ø мм
- линия обрыва (граница фрагмента)
- граница фрагмента на плане (Фр. N)

Профиль выпусков К1 (до врезки в стояк)

Выпуск	Прибор	Ø	L, м	i, мм/м	Δh, мм	Прокладка, мм
К1-1	С_01 унитаз подвесной	Ø110	1,08	20	22	короб 170×140
К1-2	С_02 умывальник	Ø50	3,19	25	80	короб 160×110
К1-3	П3 мойка кухонная	Ø50	2,30	25	58	над полом за приборами
К1-4	П4 посудомоечная машина	Ø40	2,10	30	63	над полом за приборами

Короб h×b: h — от чистого пола, b — от чистовой стены. Стяжка 35 мм — лист полов.

Узел ввода В1, Т3 (схема, без масштаба)

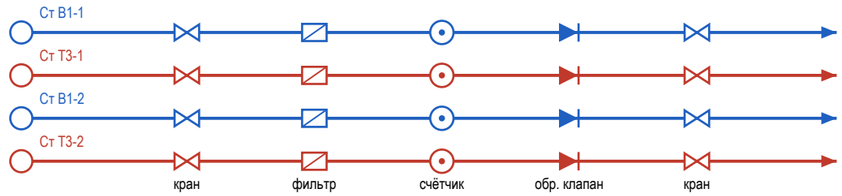

⊗ Ст К1-1, Ст К1-2 (кухня): ревизия на стояке — люк в коробе


Примечания

1. Трассы принципиальные, построены от стояков вдоль стен помещений; фактическое положение фиксируется исполнительной схемой с привязками (фото с рулеткой) до закрытия.
2. Уклон К1 не менее 1/d и не более 150 мм/м (СП 30.13330.2020, п. 19.1), приняты практические уклоны; поворот — двумя отводами 45°, ревизия после поворота, доступ сохранить. Стояк К1 в коробе — звукоизоляция стояка в коробе, без жёсткого контакта короба с трубой.
3. Решение по К1: стяжка 35 мм не укрывает трубы (нужно Ø + Δh + 45 мм) — выпуски идут над чистым полом вдоль стен: К1-3, К1-4 — за приборами и в раме инсталляции; К1-1, К1-2 — в коробе ГКЛВ под плитку (размеры в профиле). Короба — на развёртках; отметку низа врезки в стояк замерить до черновых работ.
4. На каждом вводе В1 и Т3 — кран шаровой, фильтр, счётчик, обратный клапан; доступ через люк не меньше 300×400. Водопровод — в штробе стен или в коробах; трубы испытать давлением до закрытия (акт скрытых работ).
5. Расчёт систем, диаметры магистралей и подбор оборудования выполняет проектная организация; врезка и перенос стояков — по согласованию с управляющей организацией. Арматуру и привязки сверить по паспортам приборов.


					Проект: Дом 120 м²
	Лист	№ док.	Подпись	Дата	Схема разводки водопровода и канализации · 1-й этаж
Дизайнер	Кырлан А.С.			19.10.26	

Стадия	Лист	Листов
П	23	128

План квартиры (М 1:200)

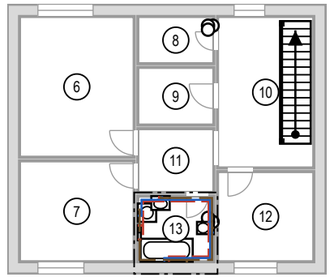

Фр. 1. Санузел второго этажа (М 1:20)

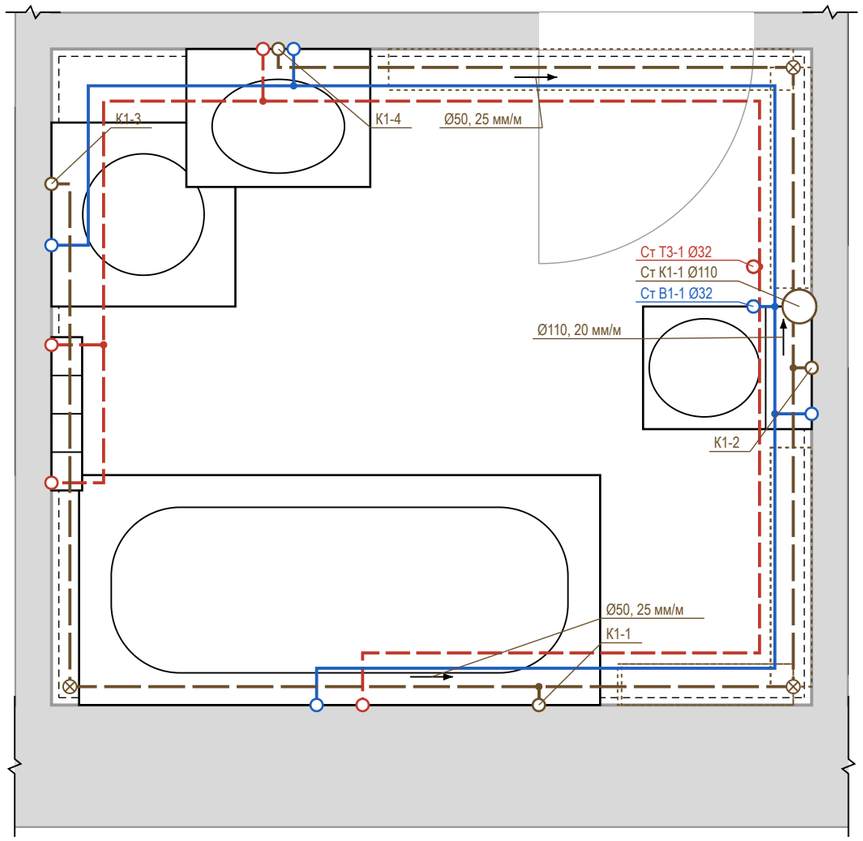

Условные обозначения

- В1 — водопровод хозяйственно-питьевой (ХВС), PP-R Ø20
- Т3 — горячее водоснабжение, подача (ГВС), PP-R Ø20
- К1 — канализация бытовая
- направление уклона К1 / пола: Ø, мм на 1 м
- ревизия (прочистка) К1 — доступ сохранить
- тройник (ответвление к прибору)
- короб К1 над чистым полом (ГКЛВ под плитку)
- вывод В1 (код — в ведомости привязок)
- вывод Т3 (код — в ведомости привязок)
- вывод К1 (код — в ведомости привязок)
- сантехприбор по расстановке (габарит модели)
- стояк «Ст К1-N / Ст В1-N» (ГОСТ 21.601), Ø мм
- линия обрыва (граница фрагмента)
- граница фрагмента на плане (Фр. N)

Профиль выпусков К1 (до врезки в стояк)

Выпуск	Прибор	Ø	L, м	i, мм/м	Δh, мм	Прокладка, мм
К1-2	С_04 унитаз подвесной	Ø110	0,28	20	6	над полом за приборами
К1-3	ОБ_02 стиральная машина	Ø50	5,32	25	133	короб 220×110
К1-4	С_05 умывальник	Ø50	2,54	25	64	под дверью — перенести выпуск
К1-1	С_03 ванна	Ø50	2,15	25	54	короб 140×110

Короб h×b: h — от чистого пола, b — от чистовой стены. Стяжка 35 мм — лист полов.

Узел ввода В1, Т3 (схема, без масштаба)

⊗ Ст К1-1, Ст К1-2 (кухня): ревизия на стояке — люк в коробе

Примечания

1. Трассы принципиальные, построены от стояков вдоль стен помещений; фактическое положение фиксируется исполнительной схемой с привязками (фото с рулеткой) до закрытия.
2. Уклон К1 не менее 1/d и не более 150 мм/м (СП 30.13330.2020, п. 19.1), приняты практические уклоны; поворот — двумя отводами 45°, ревизия после поворота, доступ сохранить. Стояк К1 в коробе — звукоизоляция стояка в коробе, без жёсткого контакта короба с трубой.
3. Решение по К1: стяжка 35 мм не укрывает трубы (нужно Ø + Δh + 45 мм) — выпуски идут над чистым полом вдоль стен: К1-2 — за приборами и в раме инсталляции; К1-3, К1-4, К1-1 — в коробе ГКЛВ под плитку (размеры в профиле). Короба — на развёртках; отметку низа врезки в стояк замерить до черновых работ.
4. Трасса К1 от К1-4 проходит под дверным проёмом — короб там невозможен: выпуск перенести или вести в полу с подъёмом пола помещения.
5. На каждом вводе В1 и Т3 — кран шаровой, фильтр, счётчик, обратный клапан; доступ через люк не меньше 300×400. Водопровод — в штробе стен или в коробах; трубы испытать давлением до закрытия (акт скрытых работ).
6. Расчёт систем, диаметры магистралей и подбор оборудования выполняет проектная организация; врезка и перенос стояков — по согласованию с управляющей организацией. Арматуру и привязки сверить по паспортам приборов.

					Проект: Дом 120 м²
	Лист	№ док.	Подпись	Дата	Схема разводки водопровода и канализации · 2-й этаж
Дизайнер	Кырлан А.С.			19.10.26	

Стадия	Лист	Листов
П	24	128

выпуск 19.10.2026 № 66b2a77b4d · стр. 24 из 128


Поз.	Наименование и техническая характеристика	Тип, марка, обозначение документа	Код продукции	Поставщик	Ед. изм.	Кол.	Масса 1 ед., кг	Примечание
	Санитарные приборы							
1	Ванна акриловая 1700×750 мм, с каркасом, экраном и отверстием слив-перелив	аналог		выбор заказчика	шт	1		С_03
2	Унитаз подвесной безободковый, с сиденьем микролифт, крепёж и звукоизолирующая прокладка	Jacob Delafon Struktura EDF102-00		выбор заказчика	шт	2		С_01, С_04
3	Инсталляция для подвесного унитаза: рама высотой 1120 мм, бачок, клавиша смыва (ось клавиши 1050 мм от чистого пола)	аналог		выбор заказчика	шт	2		С_01, С_04; короб ГКЛВ
4	Умывальник подвесной 500×400 мм, с отверстием под смеситель и переливом	аналог		выбор заказчика	шт	1		С_02
5	Умывальник подвесной 600×450 мм, с отверстием под смеситель и переливом	аналог		выбор заказчика	шт	1		С_05
6	Мойка кухонная 800×600 мм, с переливом	аналог		с кухонной мебелью	шт	1		П8
7	Полотенцесушитель водяной (ГВС), с байпасом и кранами	аналог		выбор заказчика	шт	1		С_06
	Смесители, сифоны и арматура приборов							
8	Смеситель для ванны настенный однорычажный, межосевое 150 мм, с душевым набором (лейка, шланг, держатель)	аналог		выбор заказчика	шт	1		С_03
9	Смеситель для умывальника однорычажный, с донным клапаном	аналог		выбор заказчика	шт	2		С_02, С_05
10	Смеситель кухонный однорычажный, высокий излив	аналог		выбор заказчика	шт	1		П8
11	Обвязка ванны слив-перелив Ø40/50 с сифоном	аналог		выбор заказчика	шт	1		С_03
12	Сифон для умывальника бутылочный Ø32/40–50, с гофрой к выпуску	аналог		выбор заказчика	шт	2		С_02, С_05
13	Сифон для мойки с отводом для ПММ Ø40/50	аналог		выбор заказчика	шт	1		П8
14	Сифон для стиральной машины встраиваемый в стену Ø50, с обратным клапаном	аналог		выбор заказчика	шт	1		ОБ_02
15	Кран угловой ½"×½" с гибкой подводкой 40 см (умывальники, мойка)	аналог		выбор заказчика	шт	6		по 2 на прибор
16	Кран шаровой угловой ½"×¾" для подключения стиральной и посудомоечной машины	аналог		выбор заказчика	шт	2		ОБ_02, П9
17	Узел подключения полотенцесушителя: байпас Ду20, краны шаровые ½" ×2	аналог		выбор заказчика	шт	1		
	Трубопроводы							
18	Труба полипропиленовая PP-R PN20 Ø20×3,4 (В1)	ГОСТ 32415-2013		выбор заказчика	м	18,5	0,17	12,3 + 4,3 + 10 %
19	Труба PP-R, армированная стекловолокном, PN20 Ø20×2,8 (Т3)	ГОСТ 32415-2013		выбор заказчика	м	19	0,15	12,0 + 4,9 + 10 %
20	Труба канализационная ПП Ø40 (К1)	ГОСТ 32414-2013		выбор заказчика	м	1		0,1 + 0,6 + 10 %
21	Труба канализационная ПП Ø50 (К1)	ГОСТ 32414-2013		выбор заказчика	м	12,5		9,3 + 2,0 + 10 %
22	Труба канализационная ПП Ø110 (К1)	ГОСТ 32414-2013		выбор заказчика	м	2		1,3 + 0,4 + 10 %
	Фасонные части и выводы							
23	Отвод канализационный ПП 45° Ø50	ГОСТ 32414-2013		выбор заказчика	шт	18		2 шт. на поворот
24	Отвод канализационный ПП 45° Ø110	ГОСТ 32414-2013		выбор заказчика	шт	6		2 шт. на поворот
25	Тройник канализационный ПП 45° (врезки ветвей)	ГОСТ 32414-2013		выбор заказчика	шт	7		
26	Ревизия канализационная ПП (после поворота трассы)	ГОСТ 32414-2013		выбор заказчика	шт	6		доступ сохранить
27	Фитинги PP-R Ø20: тройники, угольники 90° (ветви и повороты В1, Т3)	ГОСТ 32415-2013		выбор заказчика	шт	36		
28	Водорозетка PP-R Ø20×½" настенная, с креплением	ГОСТ 32415-2013		выбор заказчика	шт	14		коды — лист выводов
	Узлы ввода, люки, короба							
29	Кран шаровой латунный Ду15 PN16 (отключение ввода)	аналог		выбор заказчика	шт	4		Ст В1-1, Ст Т3-1, Ст В1-2, Ст Т3-2
30	Фильтр сетчатый косой Ду15	аналог		выбор заказчика	шт	4		
31	Счётчик воды крыльчатый Ду15 (ХВ, ГВ), с поверкой	аналог		выбор заказчика	шт	4		пломба УК
32	Клапан обратный Ду15	аналог		выбор заказчика	шт	4		
33	Люк ревизионный нажимной под плитку 300×400 мм	аналог		выбор заказчика	шт	2		к стоякам и арматуре
34	Звукоизоляция стояка К1 в коробе: рулонный звукоизоляционный материал ≥ 10 мм, обмотка стояка на высоту этажа	аналог		выбор заказчика	м	5,8		Ст К1-1, Ст К1-2 (кухня)
35	Короб К1 над полом: профиль ПН/ПС, ГКЛВ 12,5 мм под плитку	аналог		выбор заказчика	м	9,9		сечение — лист разводки

Примечания

1. Форма 1 ГОСТ 21.110-2013, ширины граф изменены по п. 4.1. «Аналог» — аналог по характеристикам: модели внести до черновых работ, привязки выводов сверить по паспортам.
2. Бытовая техника не входит (показана арматура подключения), мойка — в комплекте кухни. Длины труб — трасса листа разводки + подъёмы + 10 %.
3. Стояк К1 в коробе — звукоизоляция стояка в коробе без жёсткого контакта короба с трубой.
4. Расчёт систем водоснабжения и канализации, диаметры магистралей и подбор оборудования выполняет проектная организация.

					Проект: Дом 120 м²			
	Лист	№ док.	Подпись	Дата	Спецификация сантехнического оборудования	Стадия	Лист	Листов
Дизайнер	Кырлан А.С.			19.10.26		П	25	128

выпуск 19.10.2026 № 66b2a77b4d · стр. 25 из 128

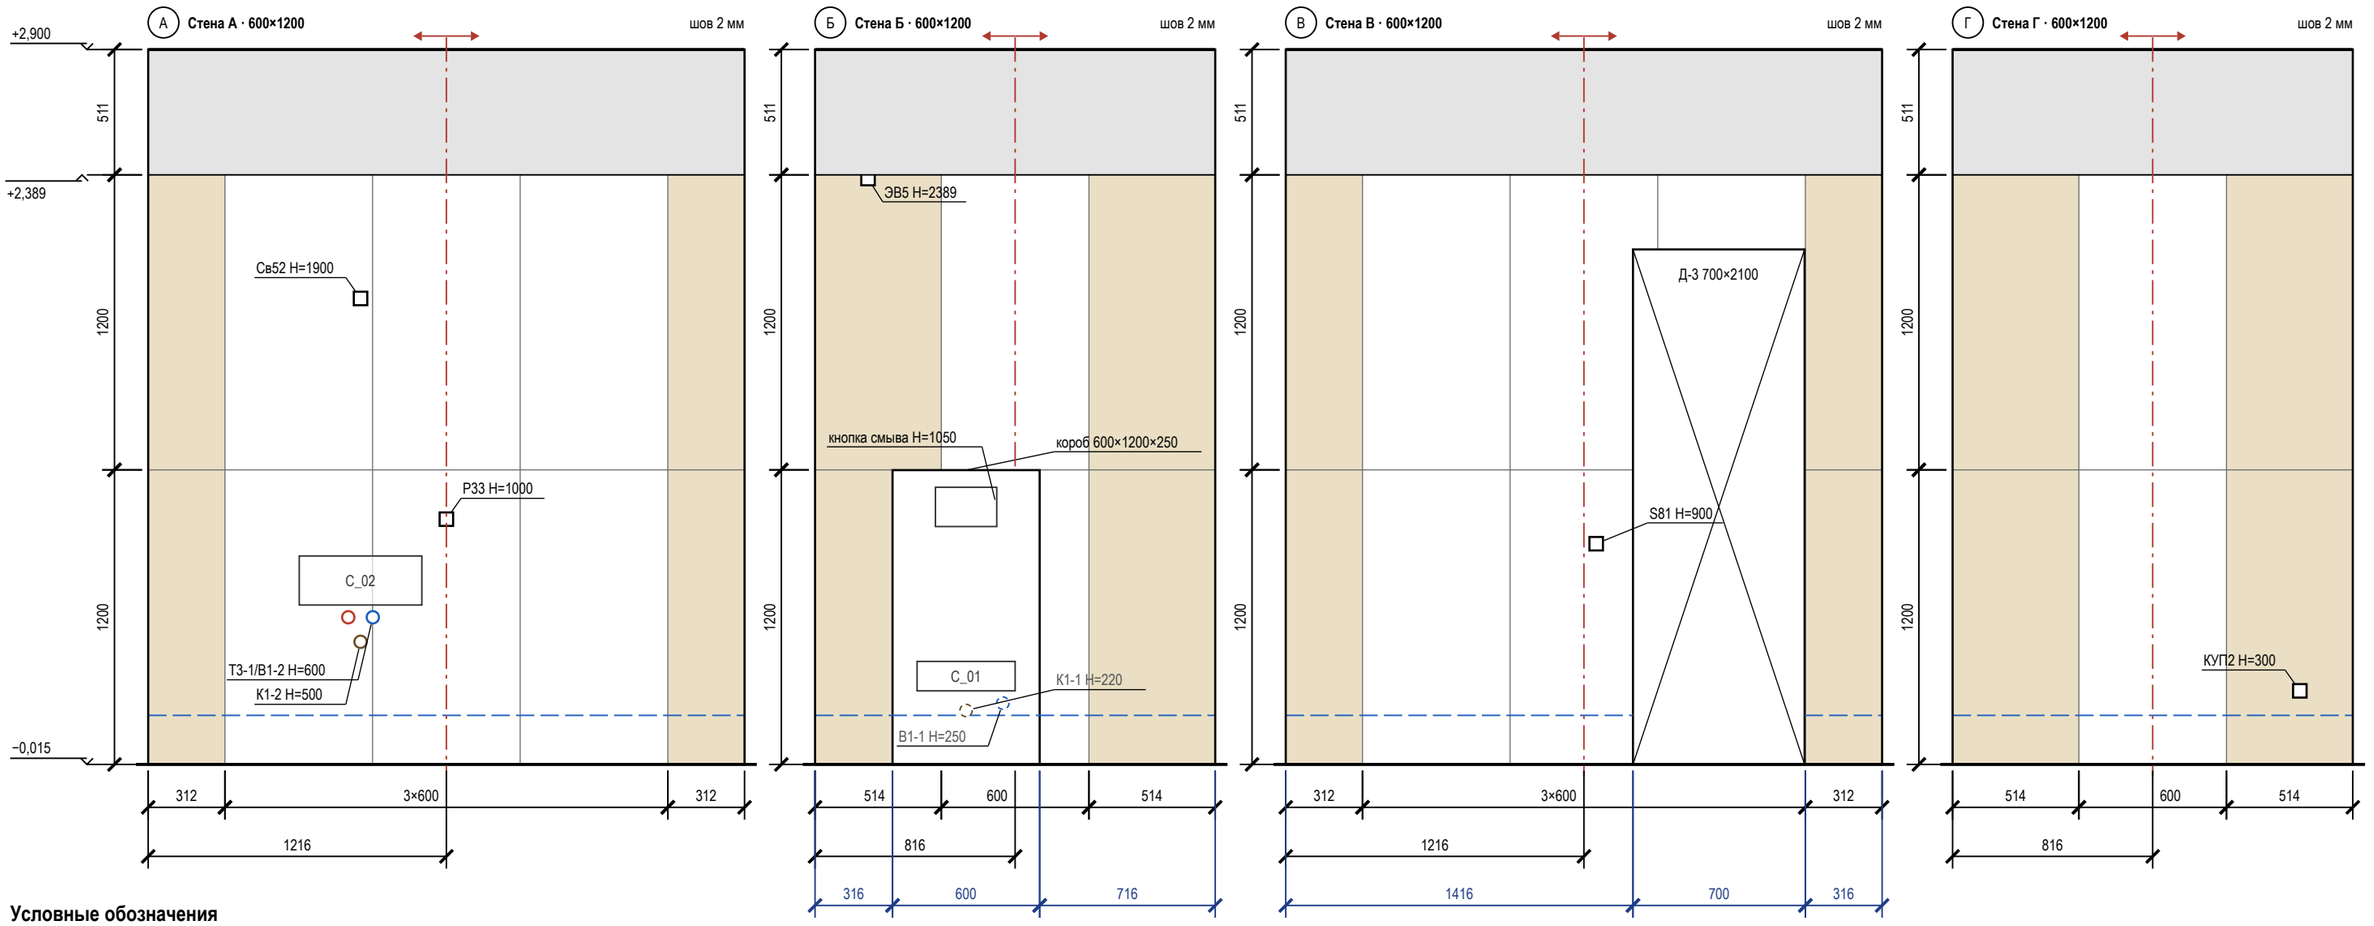

Условные обозначения

- плитка целая; тонкая линия — шов
- плитка с подрезкой (размер — на цепочке)
- ось старта; стрелки — направление укладки
- верх гидроизоляции: 200 от ЧП, в мокрой зоне — «до …»
- проём — не облицовывается
- сантехприбор: габарит, высота по практике
- короб инсталляции, в нём кнопка смыва 250×160
- вывод В1 (код — в ведомости привязок)
- вывод Т3 (код — в ведомости привязок)
- вывод К1 (код — в ведомости привязок)
- вывод за прибором / в коробе (не на сетке)
- электроточка: марка и H — по листам ЭОМ
- отметка уровня, м: ±0,000 — чистый пол жилых помещений
- низ потолка; серая полоса — стена без плитки
- (А) обозначение стены А–Г (как на развёртках)

Подсчёт плитки по стенам и коробу

Поверхность	L × H, мм	S, м²	Целых	Подр.	С запасом	Подрезки: край / верх, мм
стена А	2432 × 2404	5,96	6	4	11	312 / 312; целый ряд
стена Б	1632 × 2404	3,32	1	5	7	514 / 514; целый ряд
короб (ст. Б)	600×1200×250	1,47	1	3	5	лицо 600; бок. 250
стена В	2432 × 2404	4,49	2	8	11	312 / 312; целый ряд
стена Г	1632 × 2404	2,90	2	4	7	514 / 514; целый ряд
Итого		**18,15**	**12**	**24**	**41**	

Сдвиг точек под раскладку

Точка (ВК, ЭОМ)	Стена	Проект: от угла / H	Под раскладку: от угла / H	Сдвиг, мм
Т3-1/В1-2, К1-2, Св52	А	866 / 600, 500, 1900	915 / 600, 500, 1900	+49 на шов
ЭВ5	Б	216 / 2389	216 / 2403	H +14
S81	В	1266 / 900	1216 / 900	−50 в центр плитки


Примечания

1. Вид изнутри, стены по часовой стрелке А → Г. Высоты — от чистого пола (−0,015), отметки от ±0,000. Раскладка от чистовых размеров (штукатурка 10 + клей 5 + плитка 9 мм), подрезки чистые; старт — от оси стены, ряды от пола целыми.
2. Верх плитки +2,389, потолок +2,900, зазор 511 мм: потолок ГКЛ опустить до +2,392 (шов 3 мм, герметик) — согласовать с монтажником ГКЛ; иначе профиль-окантовка, полосу окрасить в цвет потолка. Подрезной ряд 506 мм не делать.
3. Точки из таблицы сдвигов переносятся до черновой разводки: смеситель — по оси пары В1 + Т3; вывод на оси прибора — вместе с прибором, иначе старт раскладки — на ось прибора.
4. За приборами и в коробе (В1-1, К1-1) — штриховым кольцом.
5. Гидроизоляция: 200 мм от ЧП по периметру; углы — лентой; акт скрытых работ, пролив.
6. Короб 600×1200×250: лицо 600 мм от оси кнопки смыва, боковины, полка; углы — запил 45° или профиль; за коробом плитку не кладут.

					Проект: Дом 120 м²
	Лист	№ док.	Подпись	Дата	Раскладка плитки. Санузел гостевой. Развёртки стен
Дизайнер	Кырлан А.С.			19.10.26	

Стадия	Лист	Листов
П	26	128

выпуск 19.10.2026 № 66b2a77b4d · стр. 26 из 128

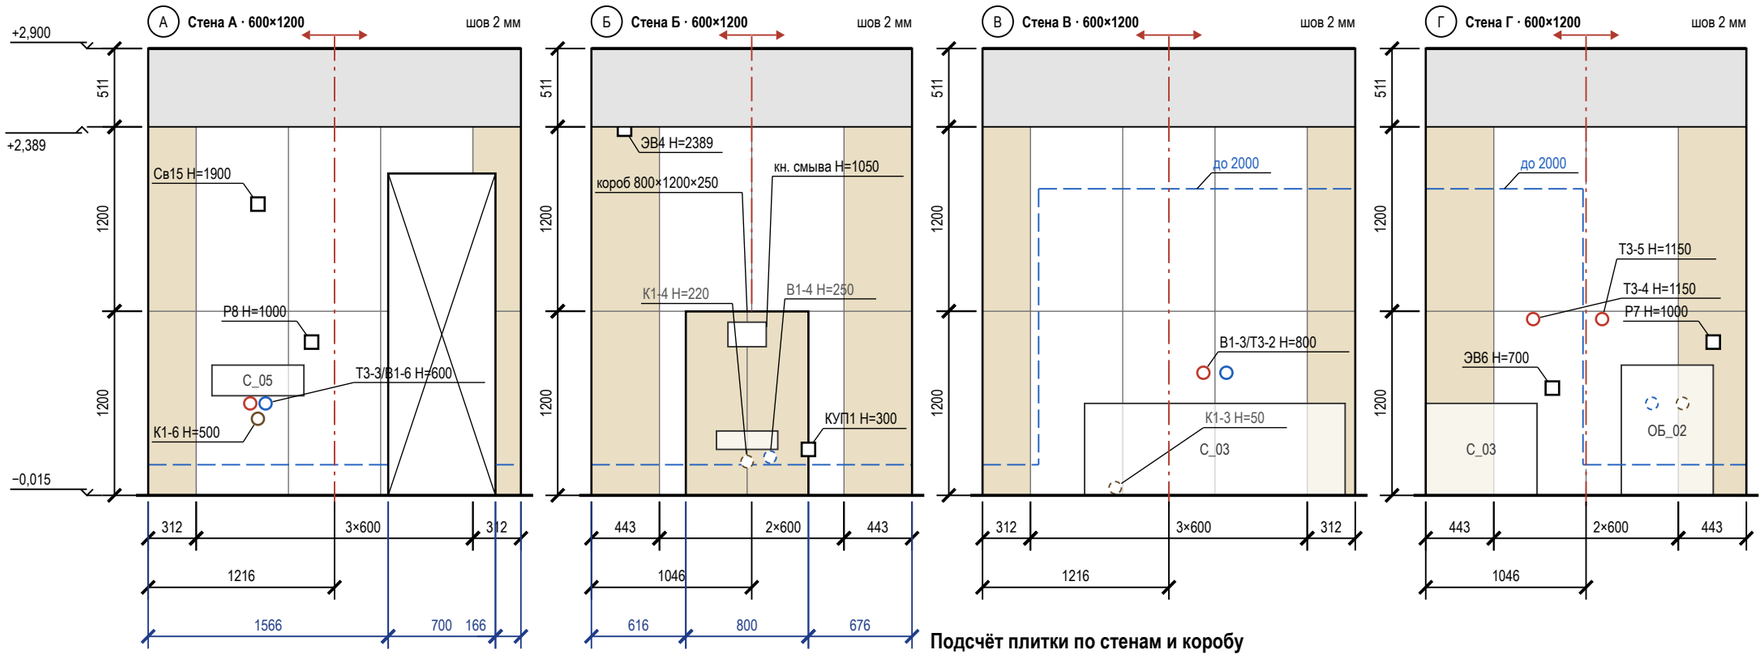

Примечания

1. Вид изнутри, стены по часовой стрелке А → Г. Высоты — от чистого пола (−0,015), отметки — от ±0,000. Раскладка от чистовых размеров (штукатурка 10 + клей 5 + плитка 9 мм), подрезки чистые; старт — от оси стены, ряды от пола целыми.
2. Верх плитки +2,389, потолок +2,900, зазор 511 мм: потолок ГКЛ опустить до +2,392 (шов 3 мм, герметик) согласовать с монтажником ГКЛ; иначе профиль-окантовка, полосу окрасить в цвет потолка. Подрезной ряд 506 мм не делать.
3. Точки из таблицы сдвигов переносятся до черновой разводки: смеситель — по оси пары В1 + Т3; вывод на оси прибора — вместе с прибором, иначе старт раскладки — на ось прибора.
4. За приборами и в коробе (В1-4, К1-4, К1-3, В1-5, К1-5) — штриховым кольцом.
5. Гидроизоляция: 200 мм от ЧП по периметру; над ванной — до 2000 и 300 мм за борт (СП 29.13330.2011, п. 7.2 — на высоту замачивания); углы — лентой; акт скрытых работ, пролив.
6. Короб 800×1200×250: лицо 399 / 399 мм от оси кнопки смыва, боковины, полка; углы — запил 45° или профиль; за коробом плитку не кладут.
7. Линии узора (швы плитки, складки штор, рёбра радиаторов) прерываются у знаков и выносок — просвет между линиями не менее 0,7 мм.

Подсчёт плитки по стенам и коробу

Поверхность	L × H, мм	S, м²	Целых	Подр.	С запасом	Подрезки: край / верх, мм
стена А	2432 × 2404	4,49	4	6	11	312 / 312; целый ряд
стена Б	2092 × 2404	4,18	2	6	9	443 / 443; целый ряд
короб (ст. Б)	800×1200×250	1,76	0	6	7	лицо 399 / 399; бок. 250
стена В	2432 × 2404	5,96	6	4	11	312 / 312; целый ряд
стена Г	2092 × 2404	3,46	4	4	9	443 / 443; целый ряд
Итого		**19,86**	**16**	**26**	**47**	

Сдвиг точек под раскладку

Точка (ВК, ЭОМ)	Стена	Проект: от угла / Н	Под раскладку: от угла / Н	Сдвиг, мм
Т3-3/В1-6, К1-6, Св15	А	716 / 600, 500, 1900	614 / 600, 500, 1900	−102 в центр плитки
Р8	А	1066 / 1000	1216 / 1000	+150 в центр плитки
ЭВ4	Б	216 / 2389	143 / 2403	−73 в центр плитки; Н +14
КУП1	Б	1416 / 300	1347 / 300	−69 в центр плитки
Т3-4	Г	701 / 1150	745 / 1150	+44 в центр плитки
Т3-5	Г	1151 / 1150	1046 / 1150	−105 на шов
Р7	Г	1876 / 1000	1949 / 1000	+73 в центр плитки
ЭВ6	Г	826 / 700	745 / 700	−81 в центр плитки


Условные обозначения

- плитка целая; тонкая линия — шов
- плитка с подрезкой (размер — на цепочке)
- ось старта; стрелки — направление укладки
- верх гидроизоляции: 200 от ЧП, в мокрой зоне — «до …»
- проём — не облицовывается
- сантехприбор: габарит, высота по практике
- короб инсталляции, в нём кнопка смыва 250×160
- вывод В1 (код — в ведомости привязок)
- вывод Т3 (код — в ведомости привязок)
- вывод К1 (код — в ведомости привязок)
- вывод за прибором / в коробе (не на сетке)
- электроточка: марка и Н — по листам ЭОМ
- отметка уровня, м: ±0,000 — чистый пол жилых помещений
- низ потолка; серая полоса — стена без плитки
- А — обозначение стены А–Г (как на развёртках)

					Проект: Дом 120 м²
	Лист	№ док.	Подпись	Дата	
Дизайнер	Кырлан А.С.			19.10.26	Раскладка плитки. Санузел второго этажа. Развёртки стен

Стадия	Лист	Листов
П	27	128

выпуск 19.10.2026 № 66b2a77b4d · стр. 27 из 128

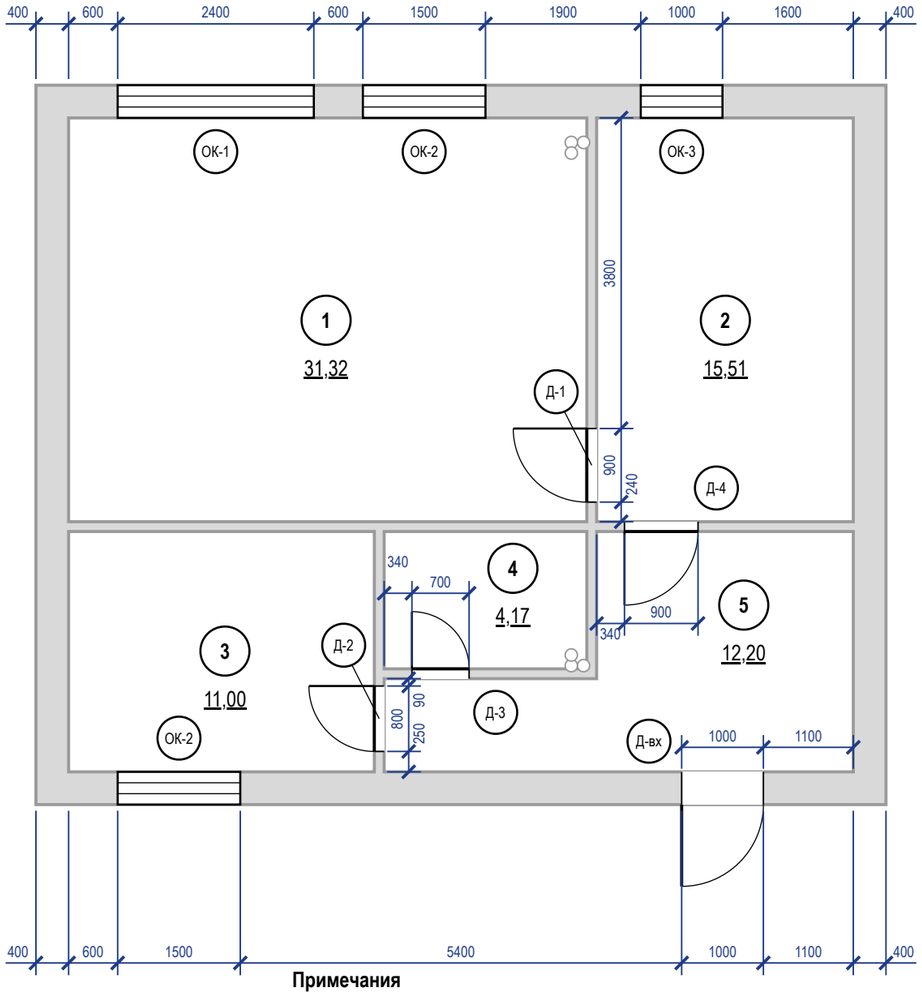

Ведомость заполнения проёмов

Марка	Наименование, обозначение	Проём ш×в, мм	Кол.	Откр.	Отделка полотна	Фурнитура	Прим.
Д-вх	Блок дверной входной, ГОСТ 31173-2016	1000×2100	1	Л	в комплекте блока	в комплекте блока (замки, глазок)	наружу
Д-1	Дверь скрытого монтажа, ТУ изготовителя	900×2100	1	Л	окраска G503 с двух сторон	скрытые петли 3D, магнитный замок	
Д-2	Дверь скрытого монтажа, ТУ изготовителя	800×2100	1	Л	окраска G503 с двух сторон	скрытые петли 3D, магнитный замок	
Д-3	Дверь скрытого монтажа, ТУ изготовителя	700×2100	1	П	в тон облицовки — пом. 4, G503 — пом. 5	скрытые петли 3D, магнитный замок, фиксатор WC	порог 15
Д-4	Дверь скрытого монтажа, ТУ изготовителя	900×2100	1	Л	окраска G503 с двух сторон	скрытые петли 3D, магнитный замок	
ОК-1	Блок оконный, ГОСТ 23166-2021; стекло — триплекс	2400×1900	1				низ 500
ОК-2	Блок оконный, ГОСТ 23166-2021	1500×1500	2				низ 900
ОК-3	Блок оконный, ГОСТ 23166-2021	1000×1500	1				низ 900


Примечания

1. Размеры проёмов и привязки — в миллиметрах от чистых граней стен до отделки; привязка — от угла того помещения, со стороны которого стоит размер. Размер в ведомости — ширина × высота проёма от чистого пола 0,000. Откос от угла помещения до проёма с коробкой — не менее 50 мм.
2. Марки в кружках — типы заполнения проёмов (ГОСТ 21.501-2018, п. 5.3.2); одна марка — один типоразмер; количество сверено с планом.
3. Открывание: Л — петли слева, П — справа, если смотреть со стороны, куда открывается полотно (на себя).
4. Остекление окон: ОК-1 (пом. 1) — триплекс. Тип стекла указать при заказе оконных блоков; замена на другое стекло — только по согласованию с автором проекта.
5. ОК-1: низ остекления 500 мм — ниже 900 мм от чистого пола, поэтому окно заказывать с безопасным стеклом (триплекс); ограждение проёма в проекте не задано (СП 54.13330.2022, п. 6.4.9; ГОСТ Р 56926).
6. Скрытые двери (Д-1…Д-4): проём замерить в чистоте; блок заказать до штукатурки (≈ 30 дн.), короб ставить до штукатурки; полотно навесить после чистовой отделки, красить в цвет стен. Порядок практика монтажа, изготовитель подтверждает.
7. Д-1…Д-4 — существующие проёмы, до техзаключения не расширять.

					Проект: Дом 120 м²
	Лист	№ док.	Подпись	Дата	План размещения дверей · 1-й этаж
Дизайнер	Кырлан А.С.			19.10.26	

Стадия	Лист	Листов
П	28	128

выпуск 19.10.2026 № 66b2a77b4d · стр. 28 из 128

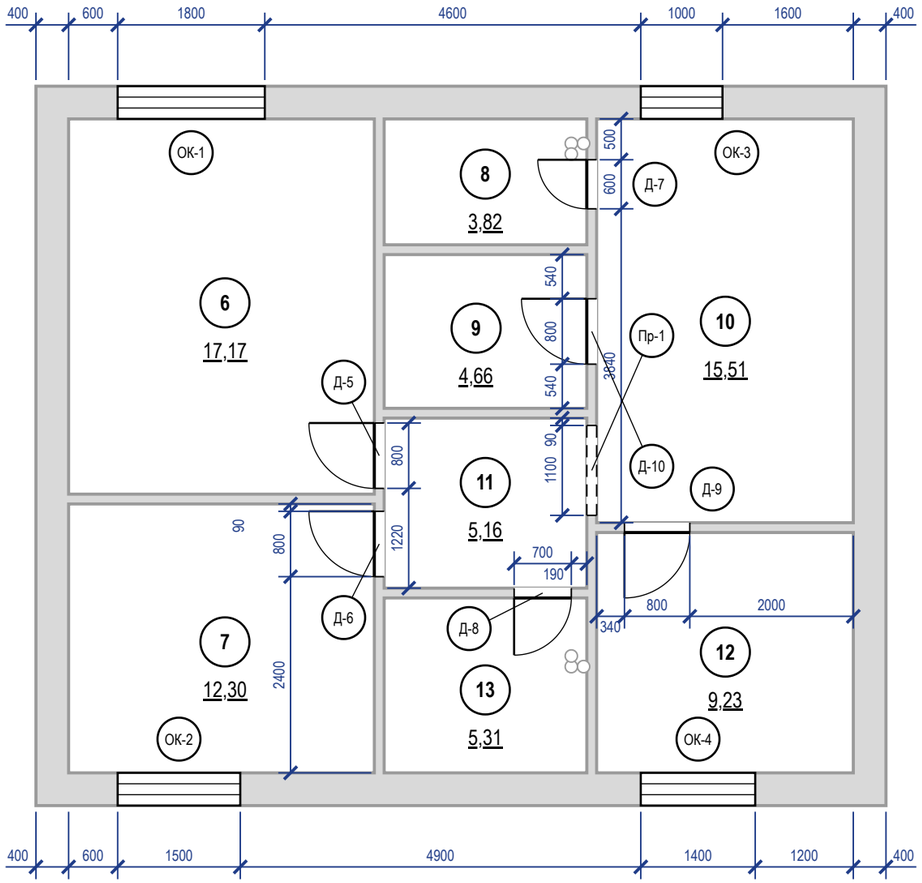

Ведомость заполнения проёмов

Марка	Наименование, обозначение	Проём ш×в, мм	Кол.	Откр.	Отделка полотна	Фурнитура	Прим.
Д-5	Дверь скрытого монтажа, ТУ изготовителя	800×2100	1	Л	окраска G503 с двух сторон	скрытые петли 3D, магнитный замок	
Д-6	Дверь скрытого монтажа, ТУ изготовителя	800×2100	1	Л	окраска G503 с двух сторон	скрытые петли 3D, магнитный замок	
Д-7	Дверь скрытого монтажа, ТУ изготовителя	600×2100	1	Л	No. 222 — пом. 8, G503 — пом. 10	скрытые петли 3D, магнитный замок	
Д-8	Дверь скрытого монтажа, ТУ изготовителя	700×2100	1	Л	в тон облицовки — пом. 13, G503 — пом. 11	скрытые петли 3D, магнитный замок, фиксатор WC	порог 15
Д-9	Дверь скрытого монтажа, ТУ изготовителя	800×2100	1	Л	окраска G503 с двух сторон	скрытые петли 3D, магнитный замок	
Д-10	Дверь скрытого монтажа, ТУ изготовителя	800×2100	1	Л	S 0502-Y — пом. 9, G503 пом. 10	скрытые петли 3D, магнитный замок	
Пр-1	Портал без заполнения	1100×2100	1				б/п
ОК-1	Блок оконный, ГОСТ 23166-2021	1800×1500	1				низ 900
ОК-2	Блок оконный, ГОСТ 23166-2021	1500×1450	1				низ 900
ОК-3	Блок оконный, ГОСТ 23166-2021	1000×1500	1				низ 900
ОК-4	Блок оконный, ГОСТ 23166-2021	1400×1450	1				низ 900


Примечания

1. Размеры проёмов и привязки — в миллиметрах от чистых граней стен до отделки; привязка — от угла того помещения, со стороны которого стоит размер. Размер в ведомости — ширина × высота проёма от чистого пола 0,000. Откос от угла помещения до проёма с коробкой — не менее 50 мм.
2. Марки в кружках — типы заполнения проёмов (ГОСТ 21.501-2018, п. 5.3.2); одна марка — один типоразмер; количество сверено с планом.
3. Открывание: Л — петли слева, П — справа, если смотреть со стороны, куда открывается полотно (на себя).
4. Скрытые двери (Д-5…Д-10): проём замерить в чистоте; блок заказать до штукатурки (≈ 30 дн.), короб ставить до штукатурки; полотно навесить после чистовой отделки, красить в цвет стен. Порядок практика монтажа, изготовитель подтверждает.
5. Д-5…Д-10 — существующие проёмы, до техзаключения не расширять.
6. Привязка проёма к углу помещения меньше 1 мм на листе, размер на плане не показан: Д-5 — 60 мм.


					Проект: Дом 120 м²			
	Лист	№ док.	Подпись	Дата	План размещения дверей · 2-й этаж	Стадия	Лист	Листов
Дизайнер	Кырлан А.С.			19.10.26		П	29	128

выпуск 19.10.2026 № 66b2a77b4d · стр. 29 из 128

План марша Л-1 (М 1:50) · 2. Холл с лестницей

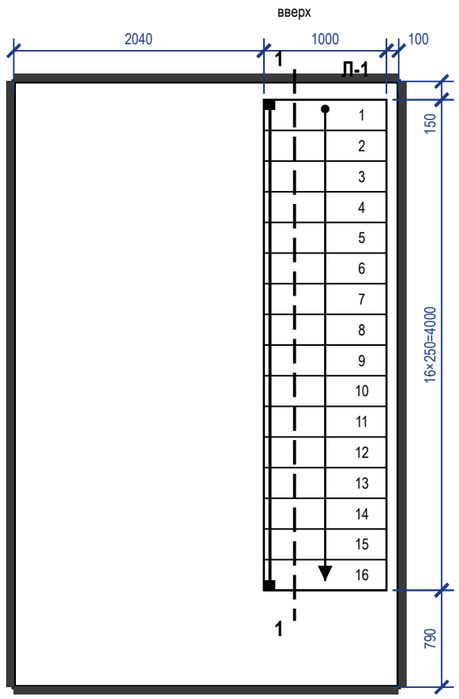


Разрез 1-1 (М 1:50)

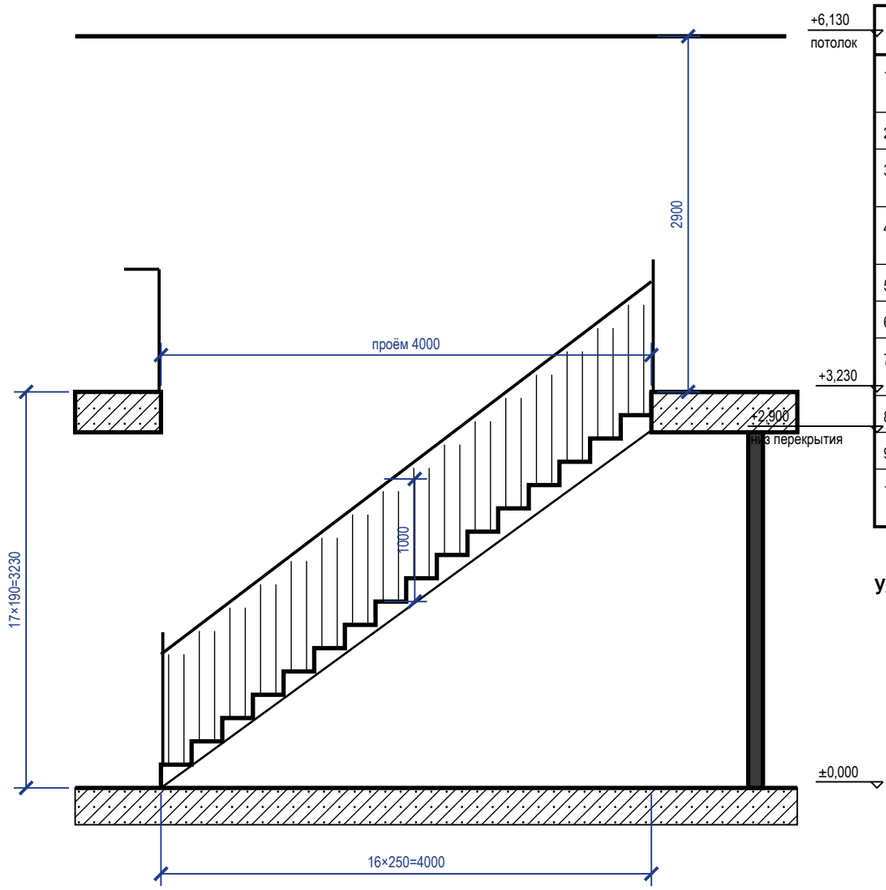

Спецификация элементов лестницы Л-1

Поз.	Наименование	Кол.	Материал, сечение	Примечание
1	Ступень (проступь)	16	дуб табак, 40 мм	1000×250, толщина по изделию
2	Подступенок	17	дуб табак	высота 190
3	Косоур	2	косоуры стальные, тёплый графит	несущие марша
4	Столб ограждения марша	2	дуб табак, стойки — графит	по концам марша, стороны Г
5	Балясина	45	дуб табак, стойки — графит	шаг 110, просвет 80
6	Поручень марша	1	Ø40	L ≈ 5,02 м, h 900
7	Столб ограждения проёма	2	дуб табак, стойки — графит	углы проёма, стороны Г
8	Балясина ограждения проёма	36	дуб табак, стойки — графит	шаг 110
9	Поручень ограждения проёма	1	Ø40	L ≈ 4,00 м, h 1000
10	Крепёж ограждения	1	комплект по изделию	нагрузка на поручень 0,5 кН/м

Узел 1. Крепление стойки ограждения (М 1:5)

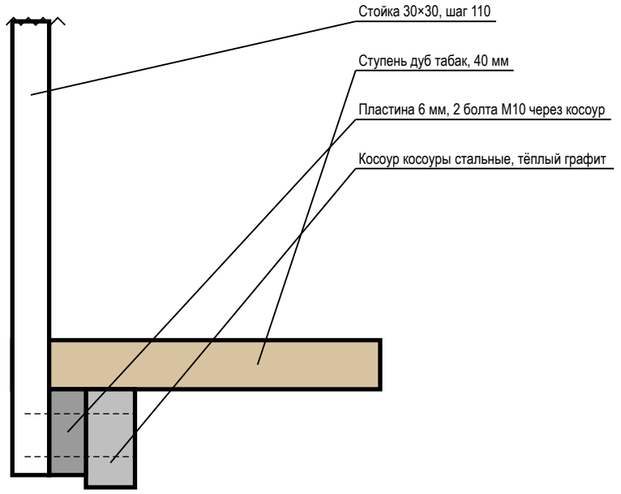

Зазор заполнения до ступени 100 (ГОСТ 25772, прил. А); узел типовой, уточнить по изделию

Примечания

1. Лестница Л-1: 17 подъёмов × 190 мм = 3230 мм (отм. ±0,000 … +3,230), проступь 250 мм, ширина марша 1000 мм; уклон 37,2°, шаг 2h + b = 630 мм (удобно 600–640 — практика).
2. Ограждение марша со стороны Г: балясины, просвет между элементами 80 мм (не больше 150 — ГОСТ 25772-2025, табл. 3, тип МВ); высота 1000 мм, поручень с одной стороны на 900 мм по линии носков (не менее 900 — СП 55.13330.2016, п. 8.3; СП 59.13330.2020, п. 6.2.11).
3. Проём в перекрытии 1000×4000 мм на этаже 2 ограждён со сторон Г высотой 1000 мм, непрерывно, с поручнем (СП 55.13330.2016, п. 8.3); нагрузка на поручень 0,5 кН/м (СП 20.13330.2016, п. 8.2.6).
4. Просвет над линией носков — не менее 2900 мм (ступень 17, под потолком мансарды); рекомендуется не менее 2000, путь эвакуации — 2200 (СП 55.13330.2016, п. 7.4).
5. Все подступенки одной высоты (СП 55.13330.2016, п. 8.2). Размеры по месту уточнить после обмера: разность отметок чистых полов замерить до заказа изделия.
6. Узел 1 — типовое решение крепления стойки к косоуру; крепёж, сечения и материал — по проекту изделия изготовителя лестницы.


	Лист	№ док.	Подпись	Дата
Дизайнер	Кырлан А.С.			19.10.26

Проект: Дом 120 м²

Лестница Л-1

Стадия	Лист	Листов
П	30	128

выпуск 19.10.2026 № 66b2a77b4d · стр. 30 из 128

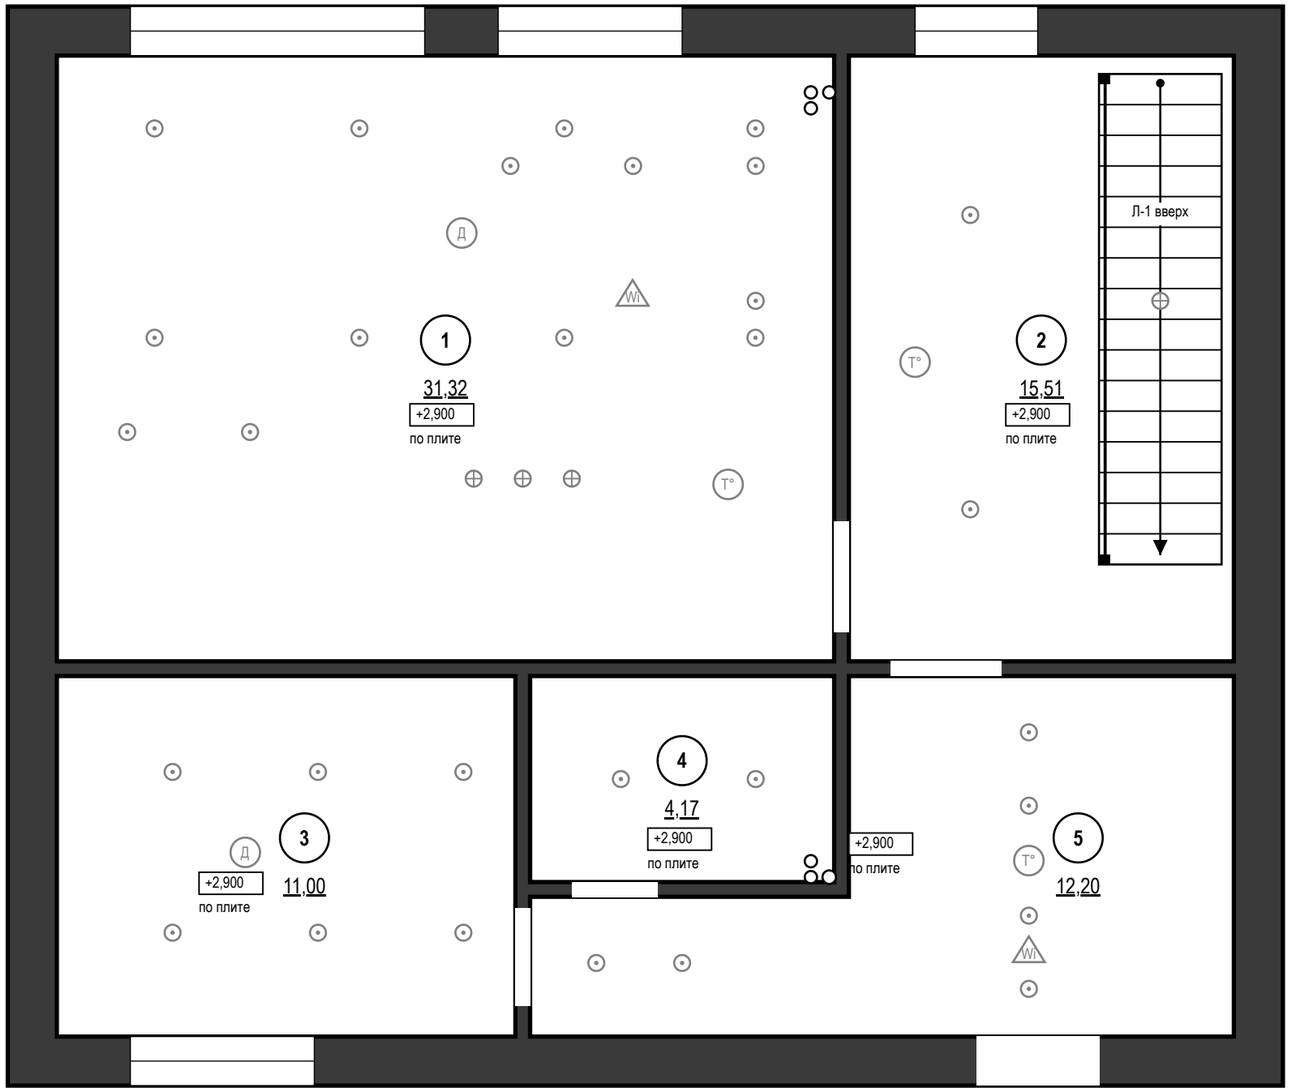

Ведомость потолков

Пом.	Марка	Конструкция	Низ	S, м²	Q
1		по плите, окраска	+2,900	31,32	
2		по плите, окраска	+2,900	15,51	
3		по плите, окраска	+2,900	11,00	
4		по плите, окраска	+2,900	4,17	
5		по плите, окраска	+2,900	12,20	
		Итого		**74,20**	

Ведомость вырезов и закладных в потолке

Марка	Устройство	Кол.	Пом.
	Светильник встраиваемый (марки — план освещения)	30	1, 2, 3, 4, 5
	Светильник подвесной (марки — план освещения)	4	1, 2
ИП4, ИП2	Извещатель дымовой	2	1, 3
ИП5, ИП6, ИП3	Извещатель тепловой	3	1, 2, 5
АР2, АР1	Точка доступа Wi-Fi, PoE	2	1, 5


Примечания

1. За отметку ±0,000 принят уровень чистого пола сухих помещений (готовое покрытие), а не существующего пола; пол пом. 4 — −0,015; верх плиты перекрытия −0,064 — расчётный по пирогу пола, не замерен; существующий пол снимается до плиты, его отметка не замерена. Отметки в прямоугольниках — низ потолка; низ плиты перекрытия +2,900. Марка потолка — одна конструкция и отметка на весь альбом.
2. Светильники и потолочные устройства — подложка с планов освещения, слаботочных систем и вентиляции (положение — по ним); вырезы и закладные — по ведомости на листе, до обшивки; отверстия не совмещать с профилями.
3. Пом. 1, 2, 3, 4, 5 — потолок по плите без подвесной системы; отделка — по ведомости отделки.

					Проект: Дом 120 м²
	Лист	№ док.	Подпись	Дата	План потолков · 1-й этаж
Дизайнер	Кырлан А.С.			19.10.26	

Стадия	Лист	Листов
П	31	128

выпуск 19.10.2026 № 66b2a77b4d · стр. 31 из 128

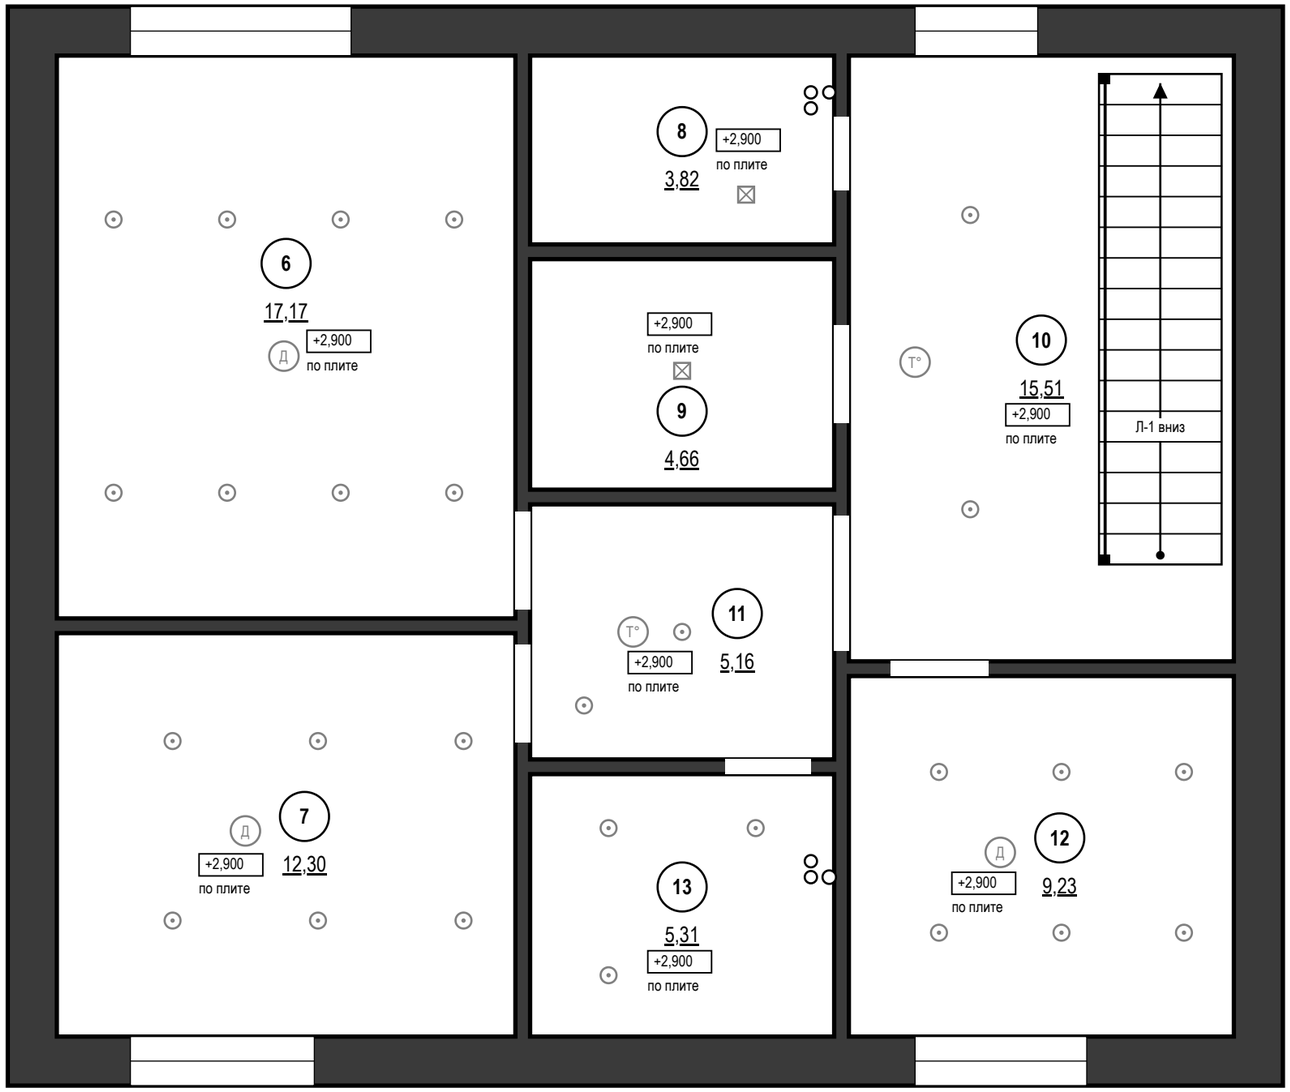

Ведомость потолков

Пом.	Марка	Конструкция	Низ	S, м²	Q
6		по плите, окраска	+2,900	17,17	
7		по плите, окраска	+2,900	12,30	
8		по плите, окраска	+2,900	3,82	
9		по плите, окраска	+2,900	4,66	
10		по плите, окраска	+2,900	15,51	
11		по плите, окраска	+2,900	5,16	
12		по плите, окраска	+2,900	9,23	
13		по плите, окраска	+2,900	5,31	
		Итого		**73,16**	

Ведомость вырезов и закладных в потолке

Марка	Устройство	Кол.	Пом.
	Светильник встраиваемый (марки — план освещения)	27	6, 7, 10, 11, 12, 13
	Светильник накладной (марки — план освещения)	2	8, 9
ИП1, ИП2, ИП2	Извещатель дымовой	3	6, 7, 12
ИП6, ИП7	Извещатель тепловой	2	10, 11


Примечания

1. За отметку ±0,000 принят уровень чистого пола сухих помещений (готовое покрытие), а не существующего пола; пол пом. 13 — −0,015; верх плиты перекрытия −0,064 — расчётный по пирогу пола, не замерен; существующий пол снимается до плиты, его отметка не замерена. Отметки в прямоугольниках — низ потолка; низ плиты перекрытия +2,900. Марка потолка — одна конструкция и отметка на весь альбом.
2. Светильники и потолочные устройства — подложка с планов освещения, слаботочных систем и вентиляции (положение — по ним); вырезы и закладные — по ведомости на листе, до обшивки; отверстия не совмещать с профилями.
3. Пом. 6, 7, 8, 9, 10, 11, 12, 13 — потолок по плите без подвесной системы; отделка — по ведомости отделки.

					Проект: Дом 120 м²
	Лист	№ док.	Подпись	Дата	План потолков · 2-й этаж
Дизайнер	Кырлан А.С.			19.10.26	

Стадия	Лист	Листов
П	32	128

выпуск 19.10.2026 № 66b2a77b4d · стр. 32 из 128

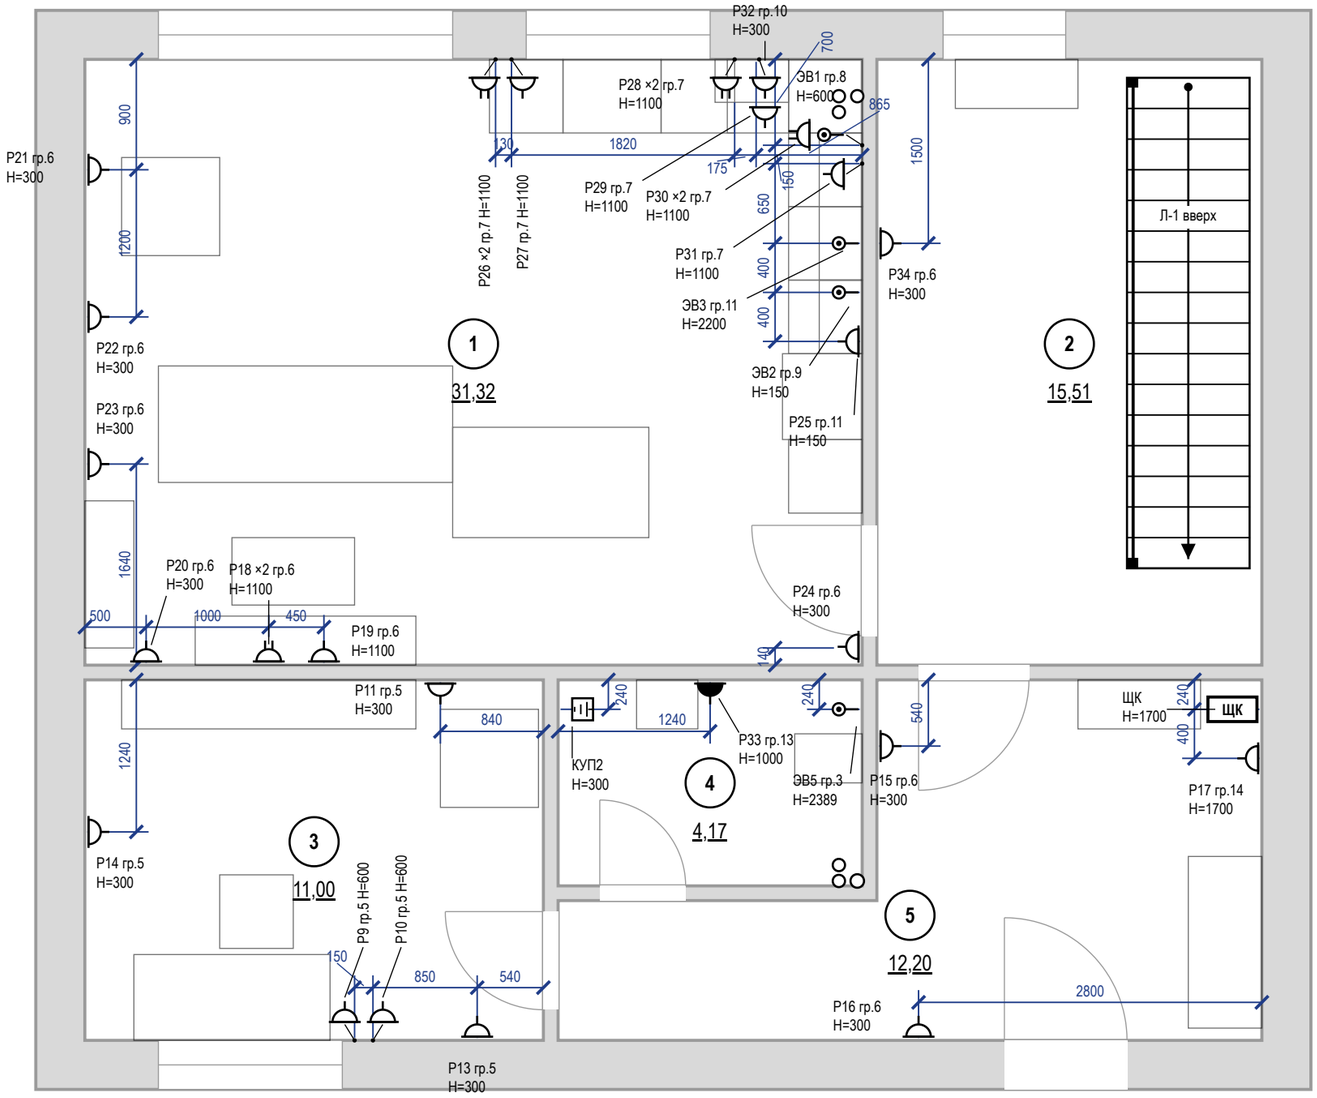

Условные обозначения


- розетка с заземляющим контактом; у знака — марка, ×N постов в рамке, гр. — группа щита, Н — высота оси, мм
- то же, рамка на 2 поста (число черточек — число постов)
- розетка влагозащищённая IP44
- вывод кабеля для подключения прибора (без розетки), марка ЭВ
- КУП — коробка уравнивания потенциалов (ДСУП), проводник к шине РЕ щита
- ЩК — щит квартирный
- знак разведён для читаемости: точка на стене — у выноски, привязка — до неё
- мебель и сантехприборы — подложка
- стояк: К1 — канализация, В1 — ХВС, Т3 — ГВС
- 1 — номер помещения, площадь м²

Примечания

1. За отметку 0,000 принят уровень чистого пола. Высоты Н — от чистого пола до оси изделия; привязки — от чистовой грани стены до оси механизма (у рамки на несколько постов — до оси рамки).
2. Высота установки, не указанная на плане: розетки — 300 мм от чистого пола; выводы кабеля — по паспорту прибора.
3. Розетки в санузле — только вне зон 0–2 (ПУЭ 7.1.48, ГОСТ Р 50571.7.701-2024), IP44, через УЗО 30 мА.
4. Розеточные и мокрые линии — через УЗО или дифавтомат с током утечки не более 30 мА (ПУЭ 7.1.79); в санузле выполнить ДСУП (ПУЭ 7.1.87–7.1.88).
5. Кабель — медный, исполнение нг(А)-LS (ГОСТ 31565-2012); скрытая прокладка только горизонтально и вертикально, фактические трассы зафиксировать исполнительной схемой до закрытия отделкой.
6. Расчёт нагрузок, токов КЗ, селективности и сечений — по проекту ЭОМ организации с допуском СРО; лист задаёт состав, расположение и группы.
7. Выводы кухонной техники — после утверждения проекта кухни (ориентировочно); привязки выводов даны от осей модулей гарнитура и пересматриваются вместе с проектом кухни.
8. Электрический тёплый пол проектом не предусмотрен; при решении заказчика устроить — отдельный лист «План тёплых полов»: контуры с отступом 100 мм от стен и мебели без ножек, датчик в гофре, терморегулятор, своя группа щита через УЗО 30 мА.
9. Ведомости электроточек, изделий, светильников и расшифровка клавиш — лист «Ведомость электроточек и изделий».

					Проект: Дом 120 м²	
	Лист	№ док.	Подпись	Дата	План розеток и электровыводов · 1-й этаж	Стадия / Лист / Листов
Дизайнер	Кырлан А.С.			19.10.26		П / 33 / 128

выпуск 19.10.2026 № 66b2a77b4d · стр. 33 из 128

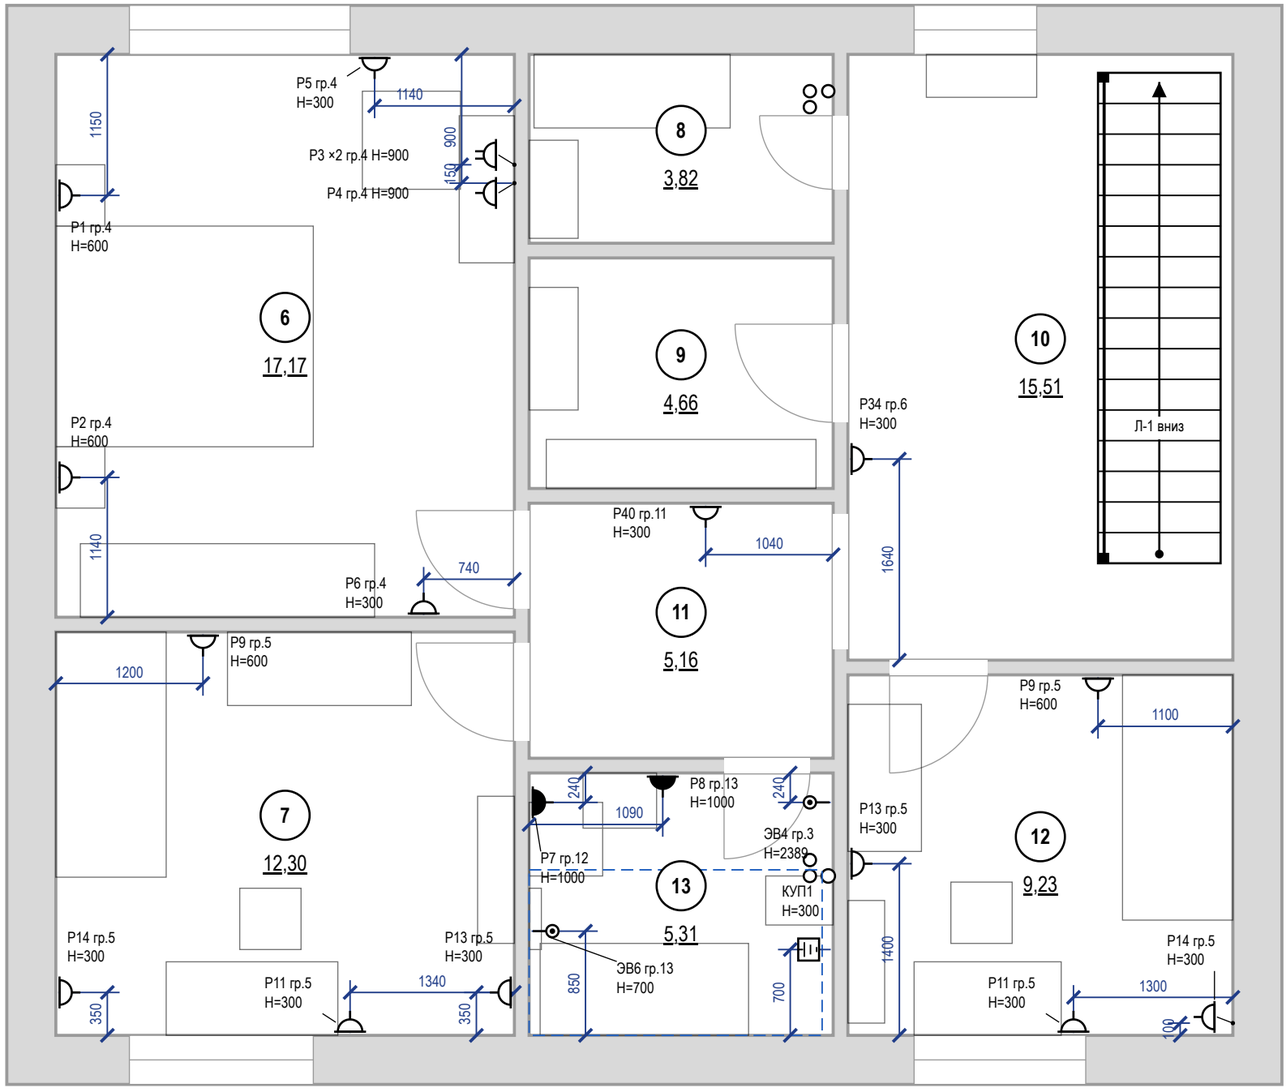

Условные обозначения


- розетка с заземляющим контактом; у знака — марка, ×N постов в рамке, гр. — группа щита, Н — высота оси, мм
- то же, рамка на 2 поста (число черточек — число постов)
- розетка влагозащищённая IP44
- вывод кабеля для подключения прибора (без розетки), марка ЭВ
- КУП — коробка уравнивания потенциалов (ДСУП), проводник к шине РЕ щита
- знак разведён для читаемости: точка на стене — у выноски, привязка — до неё
- граница зоны 2 ванной (600 мм от ванны/поддона)
- мебель и сантехприборы — подложка
- стояк: К1 — канализация, В1 — ХВС, Т3 — ГВС
- (1) номер помещения, площадь м²

Примечания

1. За отметку 0,000 принят уровень чистого пола. Высоты Н — от чистого пола до оси изделия; привязки — от чистовой грани стены до оси механизма (у рамки на несколько постов — до оси рамки).
2. Высота установки, не указанная на плане: розетки — 300 мм от чистого пола; выводы кабеля — по паспорту прибора.
3. Розетки в санузле — только вне зон 0–2 (ПУЭ 7.1.48, ГОСТ Р 50571.7.701-2024), IP44, через УЗО 30 мА.
4. Розеточные и мокрые линии — через УЗО или дифавтомат с током утечки не более 30 мА (ПУЭ 7.1.79); в санузле выполнить ДСУП (ПУЭ 7.1.87–7.1.88).
5. Кабель — медный, исполнение нг(А)-LS (ГОСТ 31565-2012); скрытая прокладка только горизонтально и вертикально, фактические трассы зафиксировать исполнительной схемой до закрытия отделкой.
6. Расчёт нагрузок, токов КЗ, селективности и сечений — по проекту ЭОМ организации с допуском СРО; лист задаёт состав, расположение и группы.
7. Электрический тёплый пол проектом не предусмотрен; при решении заказчика устроить — отдельный лист «План тёплых полов»: контуры с отступом 100 мм от стен и мебели без ножек, датчик в гофре, терморегулятор, своя группа щита через УЗО 30 мА.
8. Ведомости электроточек, изделий, светильников и расшифровка клавиш — лист «Ведомость электроточек и изделий».

					Проект: Дом 120 м²	
	Лист	№ док.	Подпись	Дата	План розеток и электровыводов · 2-й этаж	Стадия / Лист / Листов
Дизайнер	Кырлан А.С.			19.10.26		П / 34 / 128

выпуск 19.10.2026 № 66b2a77b4d · стр. 34 из 128

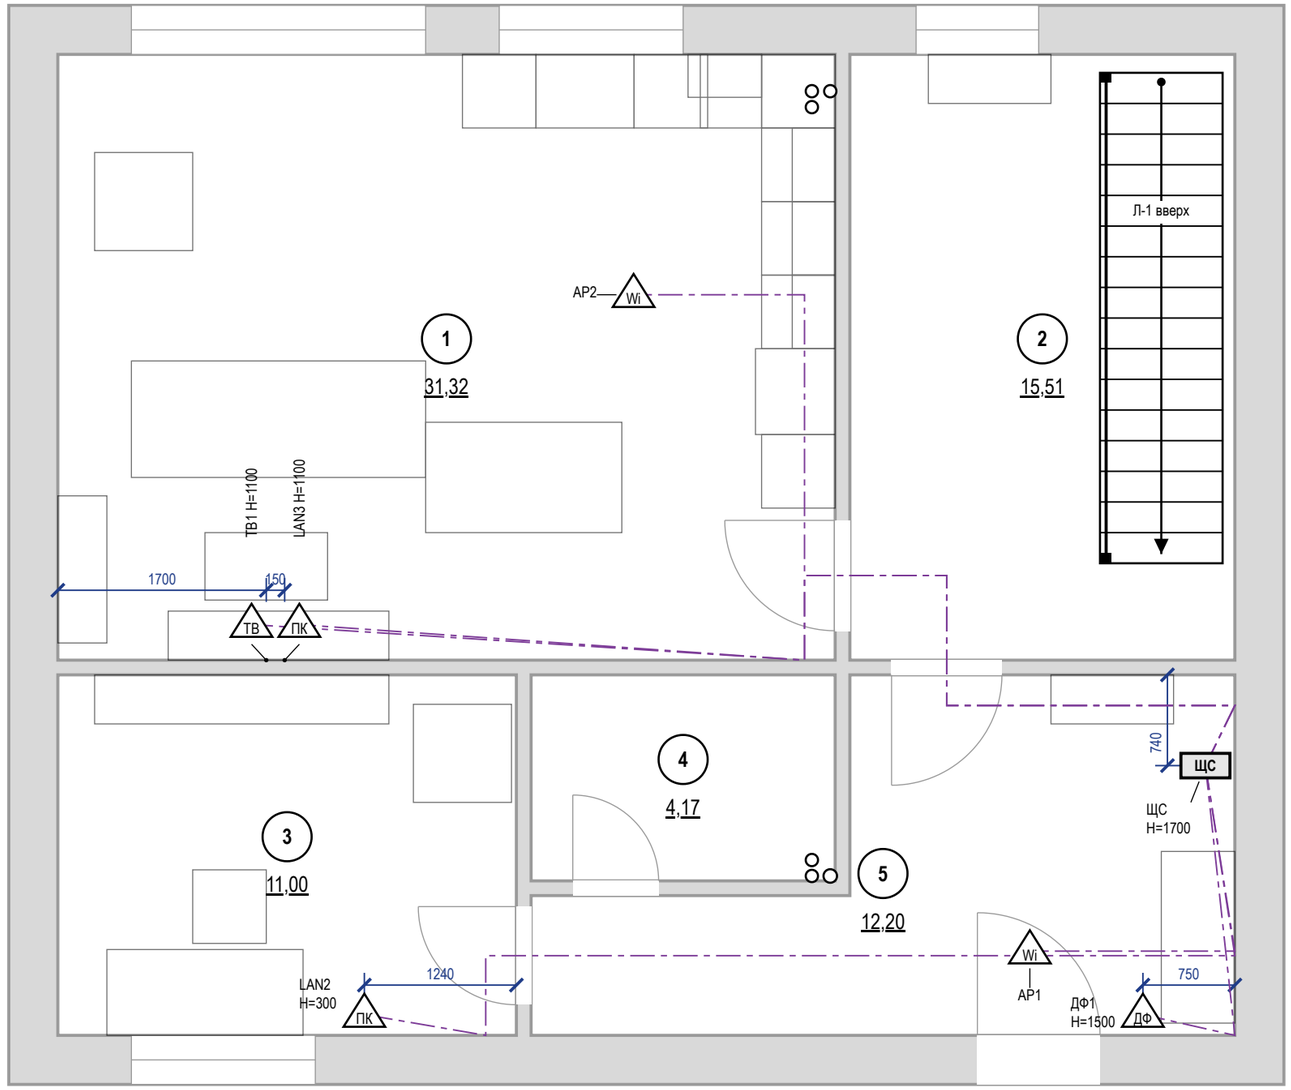


Примечания

1. За отметку 0,000 принят уровень чистого пола. Высоты H — от чистого пола до оси изделия; привязки — от чистовой грани стены до оси механизма (у рамки на несколько постов — до оси рамки).
2. Высота установки, не указанная на плане: розетки LAN и ТВ — 300 мм от чистого пола.
3. Слаботочные кабели — отдельно от силовых: в своей трубе или лотке, при параллельной прокладке не ближе 100 мм к силовым, пересечения под прямым углом; каждую точку — отдельным кабелем от ЩС без скруток.
4. Трассы на листе — принципиальные; фактические зафиксировать исполнительной схемой до закрытия отделкой. Силовые линии, УЗО 30 мА, ДСУП, кабель нг(A)-LS — по листам розеток и щита.
5. Проект силовой части и расчёт токов КЗ — по проекту ЭОМ; слаботочная часть согласуется с провайдером и управляющей компанией (домофон, коллективное ТВ).

					Проект: Дом 120 м²	
	Лист	№ док.	Подпись	Дата		
Дизайнер	Кырлан А.С.			19.10.26	План слаботочных сетей · 1-й этаж	Стадия: П; Лист: 35; Листов: 128

выпуск 19.10.2026 № 66b2a77b4d · стр. 35 из 128

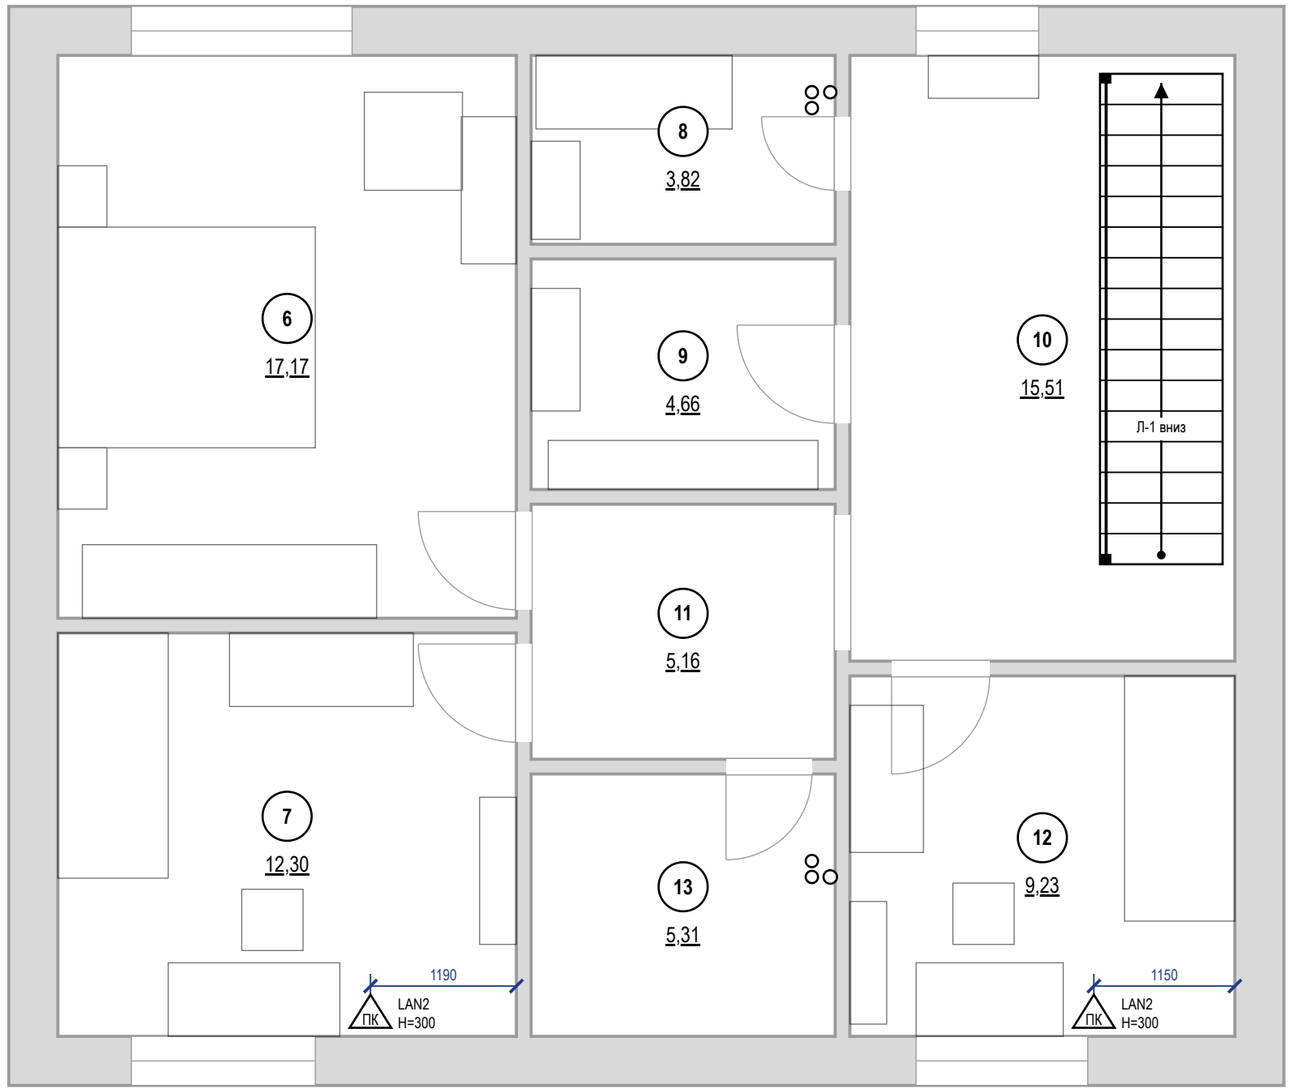


Примечания

1. За отметку 0,000 принят уровень чистого пола. Высоты H — от чистого пола до оси изделия; привязки — от чистовой грани стены до оси механизма (у рамки на несколько постов — до оси рамки).
2. Высота установки, не указанная на плане: розетки LAN и ТВ — 300 мм от чистого пола.
3. Слаботочные кабели — отдельно от силовых: в своей трубе или лотке, при параллельной прокладке не ближе 100 мм к силовым, пересечения под прямым углом; каждую точку — отдельным кабелем от ЩС без скруток.
4. Трассы на листе — принципиальные; фактические зафиксировать исполнительной схемой до закрытия отделкой. Силовые линии, УЗО 30 мА, ДСУП, кабель нг(A)-LS — по листам розеток и щита.
5. Проект силовой части и расчёт токов КЗ — по проекту ЭОМ; слаботочная часть согласуется с провайдером и управляющей компанией (домофон, коллективное ТВ).

					Проект: Дом 120 м²
	Лист	№ док.	Подпись	Дата	
Дизайнер	Кырлан А.С.			19.10.26	План слаботочных сетей · 2-й этаж

Стадия	Лист	Листов
П	36	128

выпуск 19.10.2026 № 66b2a77b4d · стр. 36 из 128

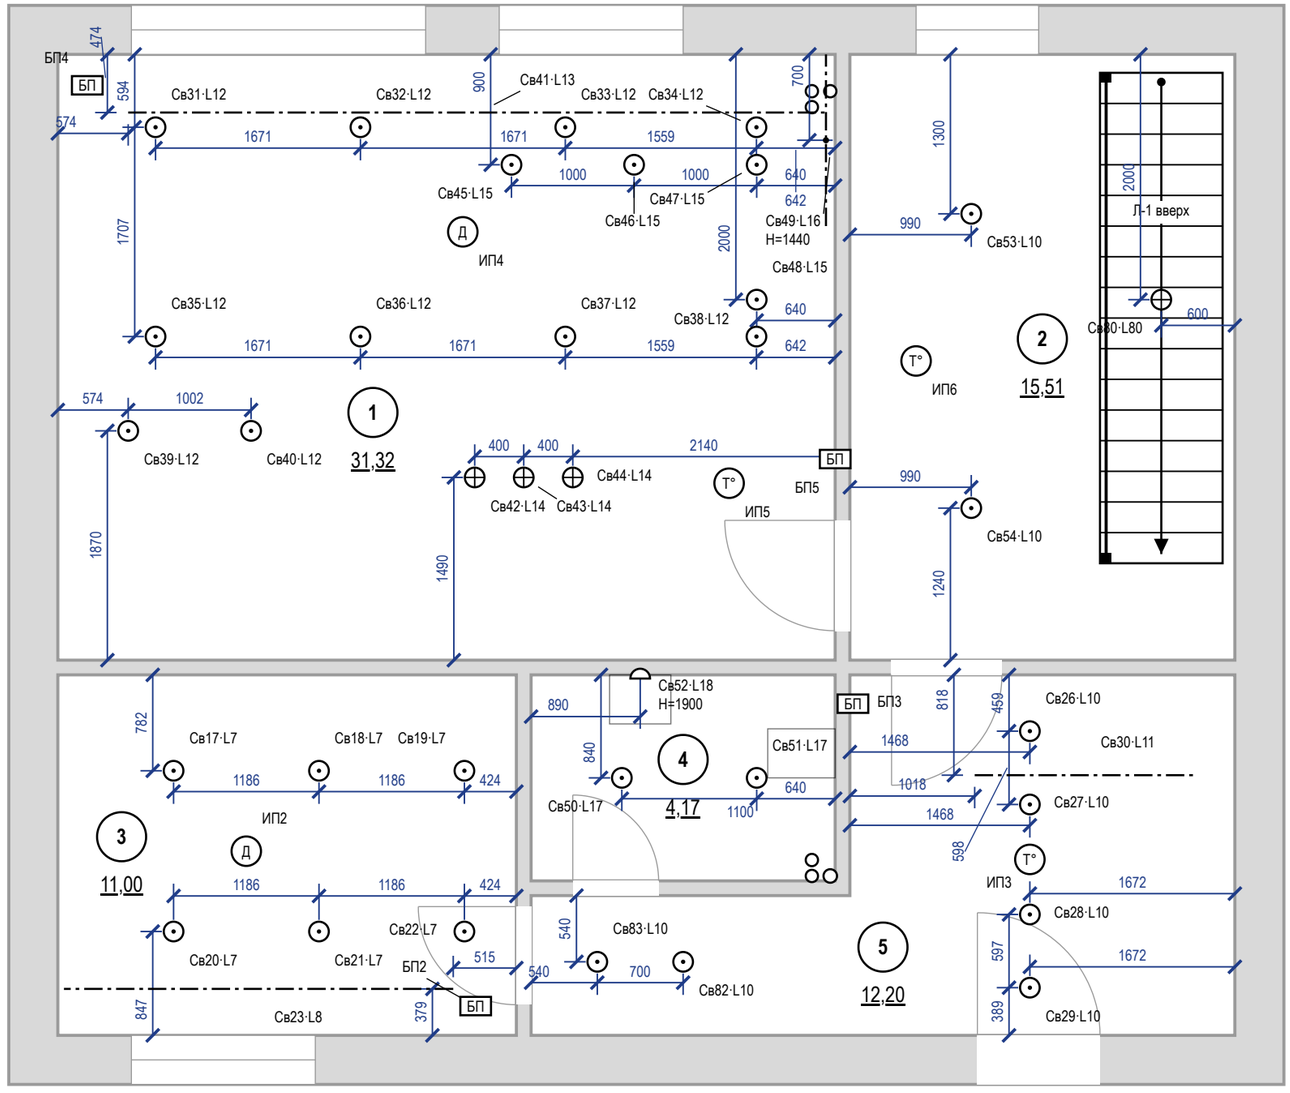


Примечания

1. За отметку 0,000 принят уровень чистого пола. Высоты H — от чистого пола до оси изделия; привязки — от чистовой грани стены до оси механизма (у рамки на несколько постов — до оси рамки).
2. Высота установки, не указанная на плане: светильники — на потолке; настенные — по отметке H у знака. Привязки — до оси светильника от чистовой грани стены, по рядам.
3. Освещённость: Eн — СанПиН 1.2.3685-21, табл. 5.52 (на полу); Ф треб. = Eн·S/(U·MF) при U = 0,5 и MF = 0,71 (СП 52.13330.2016, табл. 4.3) — оценка, не светотехнический расчёт. Декоративная подсветка в Ф не входит.
4. Во влажных помещениях — светильники не ниже IP44; в зонах 0–2 ванной — по ГОСТ Р 50571.7.701-2024 (зона 1 — IPX5).
5. Розеточные и мокрые линии — через УЗО или дифавтомат с током утечки не более 30 мА (ПУЭ 7.1.79); в санузле выполнить ДСУП (ПУЭ 7.1.87–7.1.88).
6. Кабель — медный, исполнение нг(A)-LS (ГОСТ 31565-2012); скрытая прокладка только горизонтально и вертикально, фактические трассы зафиксировать исполнительной схемой до закрытия отделкой.
7. Расчёт нагрузок, токов КЗ, селективности и сечений — по проекту ЭОМ организации с допуском СРО; лист задаёт состав, расположение и группы.
8. Ведомость светильников — лист «Ведомость электроточек и изделий».

					Проект: Дом 120 м²
	Лист	№ док.	Подпись	Дата	План освещения · 1-й этаж
Дизайнер	Кырлан А.С.			19.10.26	

Стадия	Лист	Листов
П	37	128

выпуск 19.10.2026 № 66b2a77b4d · стр. 37 из 128

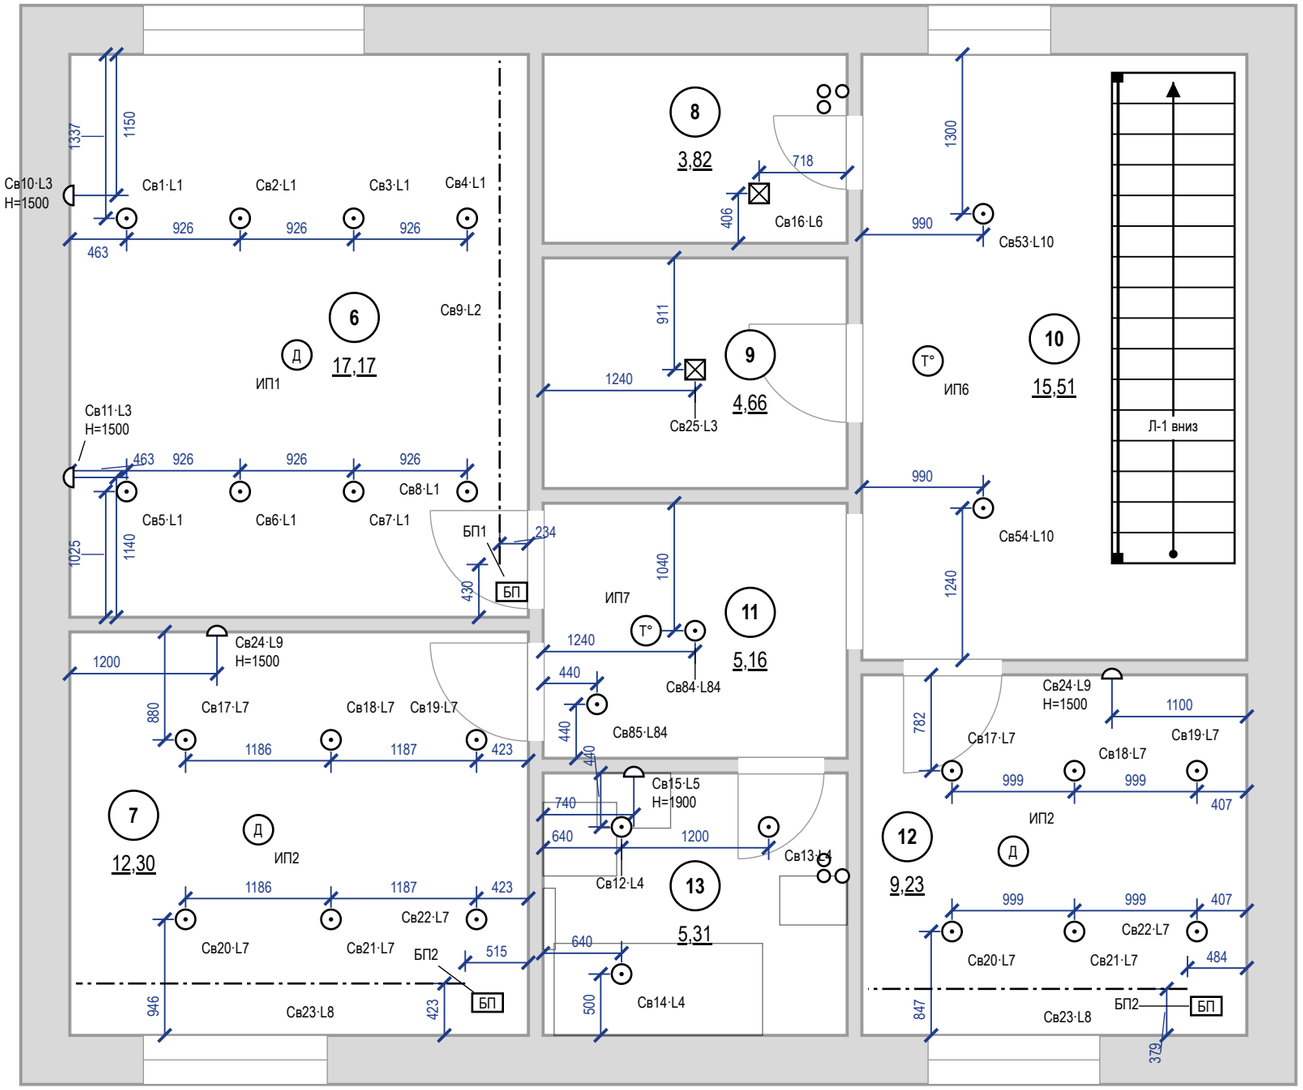

Примечания

1. За отметку 0,000 принят уровень чистого пола. Высоты Н — от чистого пола до оси изделия; привязки — от чистовой грани стены до оси механизма (у рамки на несколько постов — до оси рамки).
2. Высота установки, не указанная на плане: светильники — на потолке; настенные — по отметке Н у знака. Привязки — до оси светильника от чистовой грани стены, по рядам.
3. Освещённость: Ен — СанПиН 1.2.3685-21, табл. 5.52 (на полу); Ф треб. = Ен·S/(U·MF) при U = 0,5 и MF = 0,71 (СП 52.13330.2016, табл. 4.3) — оценка, не светотехнический расчёт. Декоративная подсветка в Ф не входит.
4. Во влажных помещениях — светильники не ниже IP44; в зонах 0–2 ванной — по ГОСТ Р 50571.7.701-2024 (зона 1 — IPX5).
5. Розеточные и мокрые линии — через УЗО или дифавтомат с током утечки не более 30 мА (ПУЭ 7.1.79); в санузле выполнить ДСУП (ПУЭ 7.1.87–7.1.88).
6. Кабель — медный, исполнение нг(A)-LS (ГОСТ 31565-2012); скрытая прокладка только горизонтально и вертикально, фактические трассы зафиксировать исполнительной схемой до закрытия отделкой.
7. Расчёт нагрузок, токов КЗ, селективности и сечений — по проекту ЭОМ организации с допуском СРО; лист задаёт состав, расположение и группы.
8. Ведомость светильников — лист «Ведомость электроточек и изделий».

					Проект: Дом 120 м²
	Лист	№ док.	Подпись	Дата	План освещения · 2-й этаж
Дизайнер	Кырлан А.С.			19.10.26	Стадия: П; Лист: 38; Листов: 128

выпуск 19.10.2026 № 66b2a77b4d · стр. 38 из 128

Спецификация светильников

Поз.	Марки	Наименование	Установка	Кол.	P, Вт	Σ P, Вт	Ф, лм	Тц, К	Ra	Угол, °	IP	Дим.	Группа	Пом.
1	Св31–Св40	Встраиваемый точечный	встраиваемый	10	12	120	1000	3000	90	—	20	да	L12	1
2	Св41	Лента светодиодная 24 В	в коробе, профиль с рассеивателем	22,1 м	9,6/м	212,2	900/м	2700	90	—	20	да	L13	1
3	Св42, Св43, Св44	Подвесной	подвес, низ H=1450	3	9	27	800	3000	90	—	20	да	L14	1
4	Св45–Св48	Встраиваемый точечный	встраиваемый	4	10	40	900	3000	90	—	20	да	L15	1
5	Св49	Линейный настенный	под верхними шкафами, H=1440	1	18	18	1500	3000	90	—	20	да	L16	1
6	Св26–Св29, Св53, Св54, Св82–Св85	Встраиваемый точечный	встраиваемый	12	7	84	600	3000	90	—	20	—	L10, L84	2, 5, 10, 11
7	Св80	Подвесной	подвес	1	12	12	1100	3000	90	—	20	—	L80	2
8	Св17–Св22	Встраиваемый точечный	встраиваемый	6	14	84	1400	2700	90	—	20	—	L7	3
9	Св23	Лента светодиодная 24 В	в коробе, профиль с рассеивателем	12,3 м	9,6/м	118,1	900/м	2700	90	—	20	да	L8	3
10	Св50	Встраиваемый точечный	встраиваемый	1	7	7	600	3000	90	—	44	—	L17	4
11	Св12–Св14, Св51	Встраиваемый точечный	встраиваемый	4	6	24	500	3000	90	—	44	—	L4, L17	4, 13
12	Св15, Св52	Настенный светильник над зеркалом, драйвер встроен	над зеркалом, H=1900	2	8	16	600	3000	90	—	44	—	L5, L18	4, 13
13	Св30	Лента светодиодная 24 В	в коробе, профиль с рассеивателем, датчик движения	1,8 м	4,8/м	8,6	150/м	2700	90	—	20	нет	L11	5
14	Св1–Св8	Встраиваемый точечный	встраиваемый	8	12	96	1000	2700	90	—	20	—	L1	6
15	Св9	Лента светодиодная 24 В	в коробе, профиль с рассеивателем	15,5 м	9,6/м	148,8	900/м	2700	90	—	20	да	L2	6
16	Св10, Св11, Св24	Настенный (бра)	на стене, H=1500	4	6	24	400	2700	90	60	20	—	L3, L9	6, 7, 12
17	Св17–Св22	Встраиваемый точечный	встраиваемый	12	11	132	1100	2700	90	—	20	—	L7	7, 12
18	Св23	Лента светодиодная 24 В	в коробе, профиль с рассеивателем	24,6 м	9,6/м	236,2	900/м	2700	90	—	20	да	L8	7, 12
19	Св16	Потолочный накладной	на потолке, засветка стены	1	10	10	900	3000	90	—	20	—	L6	8
20	Св25	Потолочный накладной	на потолке	1	9	9	600	3000	90	—	20	—	L3	9
		Итого		**70 шт + 76,3 м**		**1426,8**								

LED-ленты, линейные светильники и блоки питания

Марка	Пом.	L, м	U, В	Вт/м	Σ P, Вт	БП	P БП, Вт	Загр., %	Питание	Доступ к БП
Св41	1	22,1	24	9,6	212,2	БП4	300	71	с двух концов	люк 300×300 в коробе У1 у входа
Св49	1	3	24	—	18	БП5	60	30	встроенный ввод	в пенале M_32, верх, съёмная панель
Св23	3	12,3	24	9,6	118,1	БП2	200	177	с двух концов	люк 300×300 в коробе У1 у окна
Св30	5	1,8	24	4,8	8,6	БП3	20	43	с одного конца	в шкафу M16, верхняя полка
Св9	6	15,5	24	9,6	148,8	БП1	200	74	с двух концов	люк 300×300 в коробе У1 у входа
Св23	7	12,3	24	9,6	118,1	БП2	200	177	с двух концов	люк 300×300 в коробе У1 у окна
Св23	12	12,3	24	9,6	118,1	БП2	200	177	с двух концов	люк 300×300 в коробе У1 у окна

Сценарии освещения

Пом.	Сценарий	Группы и уровни, %	Чем включается
1	Вечер	L12 споты гостиной — 30; L13 подсветка короба — 100; L14 подвесы над столом — 50; L15 споты кухни — 0; L16 подсветка столешницы — 0	S10 светорегулятор, S11 светорегулятор
1	Ужин	L12 споты гостиной — 0; L13 подсветка короба — 60; L14 подвесы над столом — 100; L15 споты кухни — 0; L16 подсветка столешницы — 30	S10 светорегулятор, S11 светорегулятор, S12 светорегулятор
1	Кино	L12 споты гостиной — 0; L13 подсветка короба — 20; L14 подвесы над столом — 0; L15 споты кухни — 0; L16 подсветка столешницы — 0	S10 светорегулятор
1	Готовка	L12 споты гостиной — 50; L13 подсветка короба — 0; L14 подвесы над столом — 0; L15 споты кухни — 100; L16 подсветка столешницы — 100	S10 светорегулятор, S11 светорегулятор, S12 светорегулятор
3	Вечер	L7 споты — 0; L8 подсветка короба — 100; L9 бра — 100	S4, S5
6	Вечер	L1 споты — 0; L2 подсветка короба — 100; L3 бра — 100	S1, S2, S3
6	Уборка	L1 споты — 100; L2 подсветка короба — 100; L3 бра — 0	S1, S2, S3
7	Вечер	L7 споты — 0; L8 подсветка короба — 100; L9 бра — 100	S4, S5
12	Вечер	L7 споты — 0; L8 подсветка короба — 100; L9 бра — 100	S4, S5

Слои света

общий — равномерный свет помещения, по норме освещённости

рабочий — местный свет задачи: столешница, зеркало, чтение у кровати


акцентный — подсветка потолка, стен и ниш; не входит в поток общего света

ночной — путь спальня → санузел: не выше 2700 K, малая яркость, датчик движения

Примечания

1. Позиции и марки Св — те же, что на плане освещения (лист «План освещения») и в ведомости светильников (лист «Ведомость электроточек и изделий»); группы L — по плану выключателей (лист «План выключателей»).
2. Модели светильников не назначены: подбор по графам спецификации — поток, Тц, Ra, угол, IP и диммирование не хуже указанных, мощность не больше. IP 20 — сухие помещения.
3. Длина LED-ленты в карнизе — по линии карниза плана потолков (лист «План потолков»); Σ P = Вт/м × длина. Блок питания загружен не больше чем на 80 %; лента 24 В длиннее 10 м питается с двух концов; доступ к блоку питания — люк ревизии 300×300 мм или место, указанное в таблице.
4. Сценарии: уровень — доля максимальной яркости группы, %; 0 — группа выключена. Уровень ниже 100 % — только у групп на светорегуляторе (задний фронт, TE) с диммируемыми драйверами и блоками питания.
5. Мощность и поток — по паспортам принятых изделий, Σ P — установленная мощность освещения. Оценка освещённости — на плане освещения; это не светотехнический расчёт.
6. Не поместилось строк таблиц: 13 — продолжение выпустить отдельным листом.

					Проект: Дом 120 м²			
	Лист	№ док.	Подпись	Дата	Спецификация светильников и сценарии освещения	Стадия	Лист	Листов
Дизайнер	Кырлан А.С.			19.10.26		П	39	128

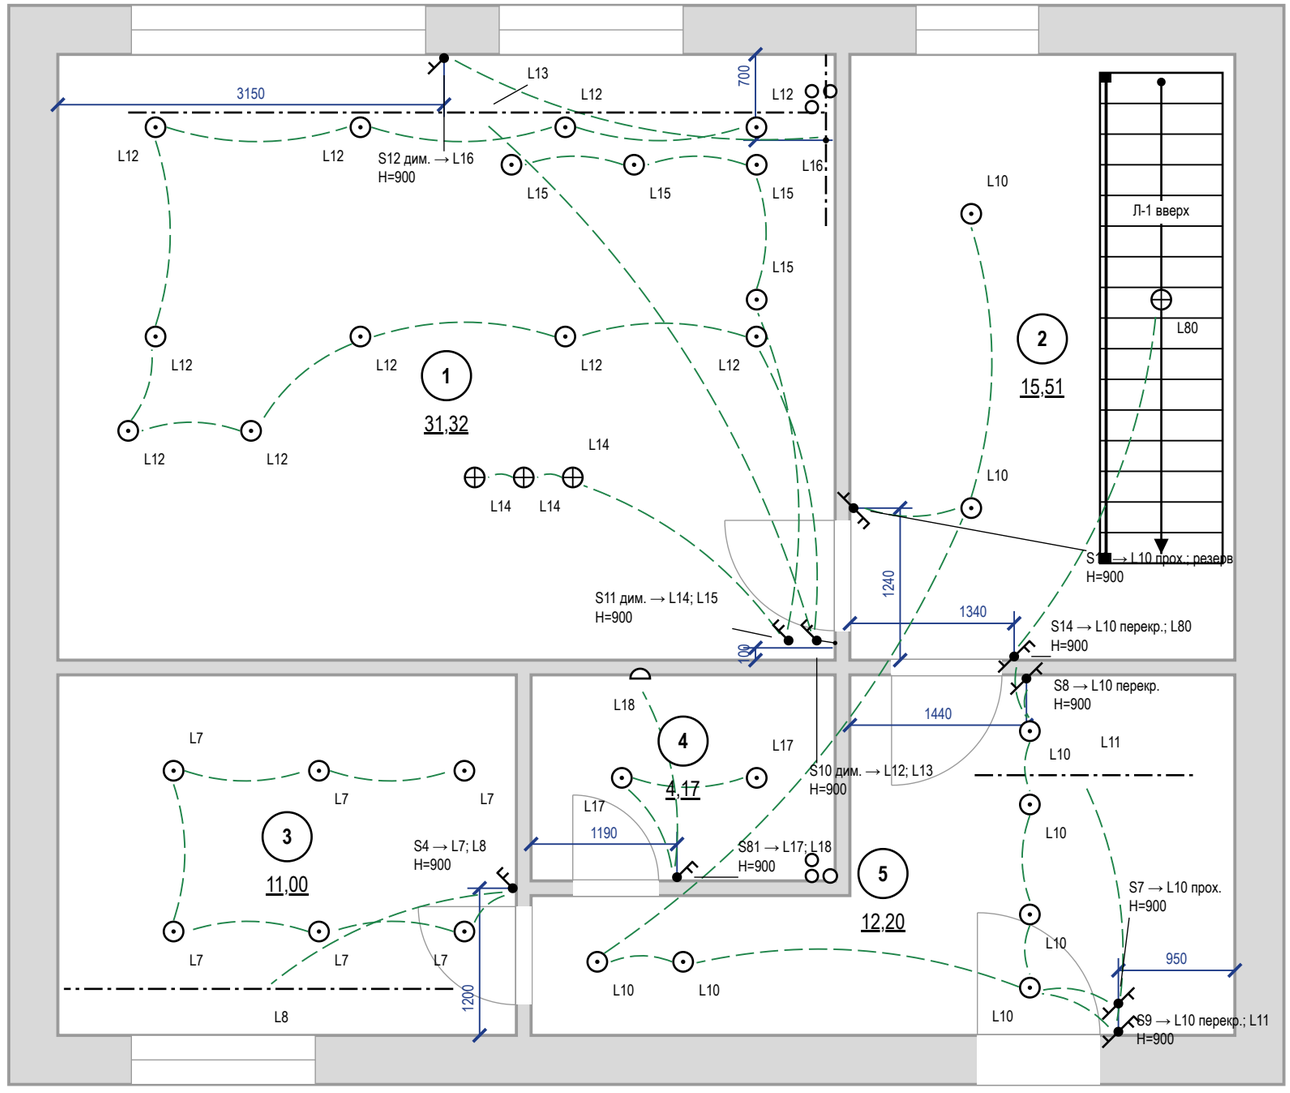


Примечания

1. За отметку 0,000 принят уровень чистого пола. Высоты H — от чистого пола до оси изделия; привязки — от чистовой грани стены до оси механизма (у рамки на несколько постов — до оси рамки).
2. Высота установки, не указанная на плане: выключатели — 900 мм от чистого пола, со стороны дверной ручки (ПУЭ 7.1.51).
3. Линии связи показывают, какой выключатель какую группу L включает; это не трасса кабеля. Трасса — принципиальная, фактическую зафиксировать исполнительной схемой.
4. Группы из нескольких мест (L10 — S7, S8, S9, S14, S16): на крайних местах — проходные клавиши, на промежуточных — перекрёстные; механизмы — в ведомости изделий.
5. Светорегулятор — по заднему фронту (для LED-драйверов), совместимость с драйверами проверить до закупки.
6. Розеточные и мокрые линии — через УЗО или дифавтомат с током утечки не более 30 мА (ПУЭ 7.1.79); в санузле выполнить ДСУП (ПУЭ 7.1.87–7.1.88).
7. Кабель — медный, исполнение нг(A)-LS (ГОСТ 31565-2012); скрытая прокладка только горизонтально и вертикально, фактические трассы зафиксировать исполнительной схемой до закрытия отделкой.
8. Расчёт нагрузок, токов КЗ, селективности и сечений — по проекту ЭОМ организации с допуском СРО; лист задаёт состав, расположение и группы.
9. Расшифровка клавиш и ведомость изделий — лист «Ведомость электроточек и изделий».

					Проект: Дом 120 м²
	Лист	№ док.	Подпись	Дата	Управление светильниками · 1-й этаж
Дизайнер	Кырлан А.С.			19.10.26	

Стадия	Лист	Листов
П	40	128

выпуск 19.10.2026 № 66b2a77b4d · стр. 40 из 128

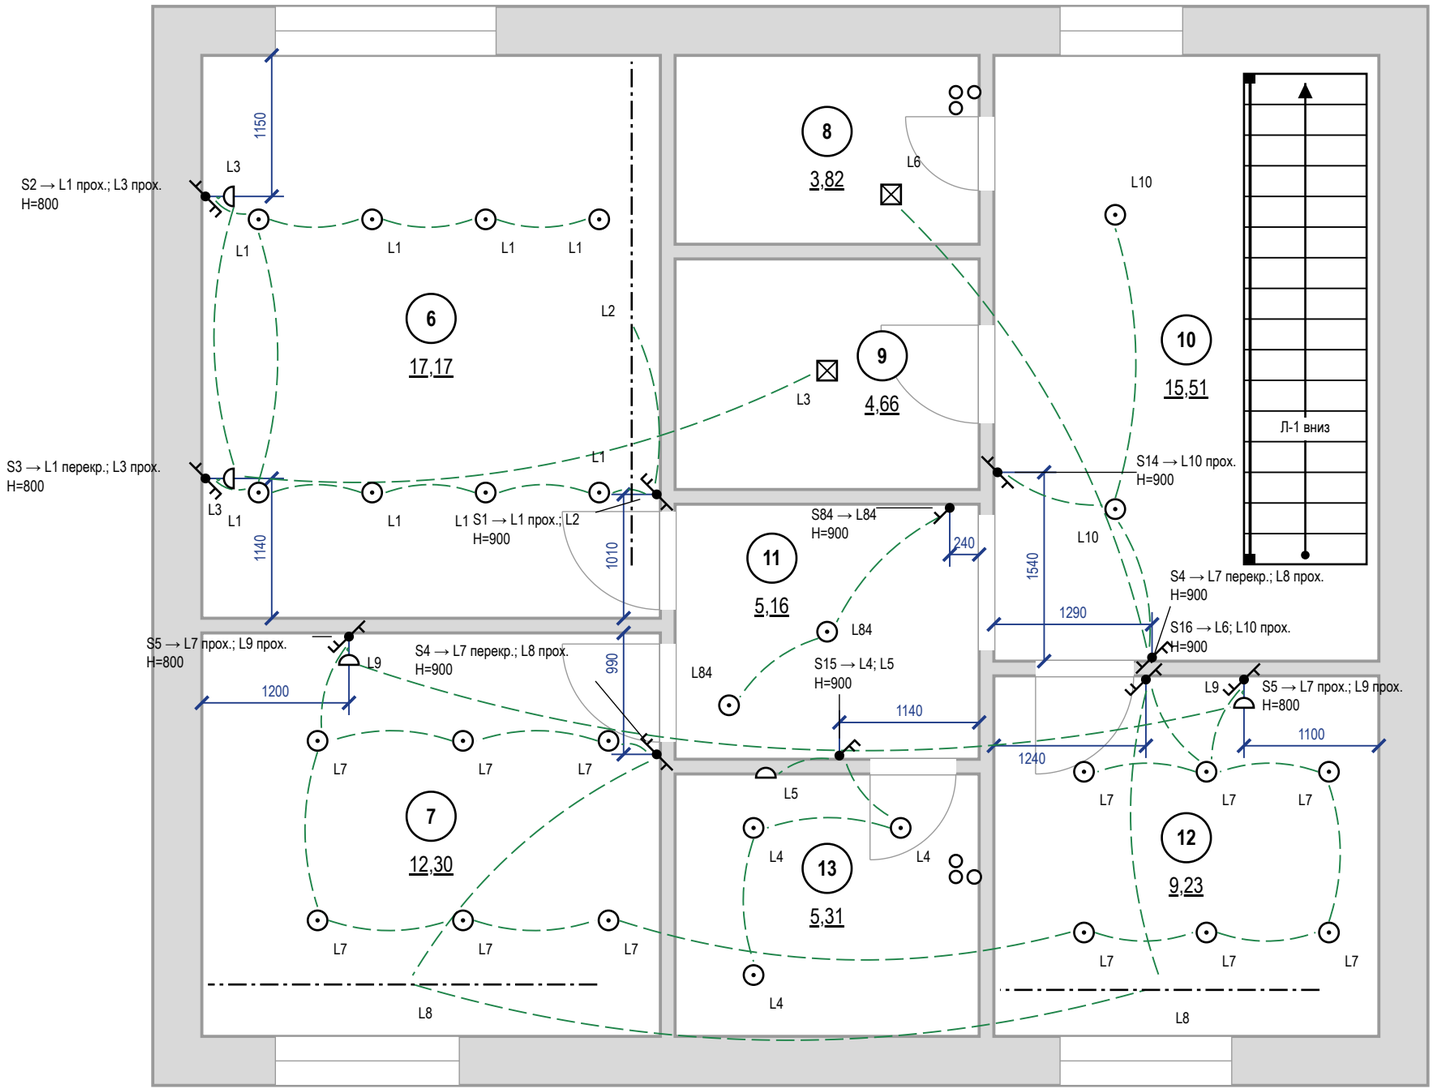


Примечания

1. За отметку 0,000 принят уровень чистого пола. Высоты H — от чистого пола до оси изделия; привязки — от чистовой грани стены до оси механизма (у рамки на несколько постов — до оси рамки).
2. Высота установки, не указанная на плане: выключатели — 900 мм от чистого пола, со стороны дверной ручки (ПУЭ 7.1.51).
3. Линии связи показывают, какой выключатель какую группу L включает; это не трасса кабеля. Трасса — принципиальная, фактическую зафиксировать исполнительной схемой.
4. Группы из нескольких мест (L1 — S1, S2, S3; L3 — S2, S3; L7 — S4, S4, S5, S5; L8 — S4, S4; L9 — S5, S5; L10 — S14, S16): на крайних местах — проходные клавиши, на промежуточных — перекрёстные; механизмы — в ведомости изделий.
5. Розеточные и мокрые линии — через УЗО или дифавтомат с током утечки не более 30 мА (ПУЭ 7.1.79); в санузле выполнить ДСУП (ПУЭ 7.1.87–7.1.88).
6. Кабель — медный, исполнение нг(A)-LS (ГОСТ 31565-2012); скрытая прокладка только горизонтально и вертикально, фактические трассы зафиксировать исполнительной схемой до закрытия отделкой.
7. Расчёт нагрузок, токов КЗ, селективности и сечений — по проекту ЭОМ организации с допуском СРО; лист задаёт состав, расположение и группы.
8. Расшифровка клавиш и ведомость изделий — лист «Ведомость электроточек и изделий».

					Проект: Дом 120 м²
	Лист	№ док.	Подпись	Дата	Управление светильниками · 2-й этаж
Дизайнер	Кырлан А.С.			19.10.26	

Стадия	Лист	Листов
П	41	128

выпуск 19.10.2026 № 66b2a77b4d · стр. 41 из 128

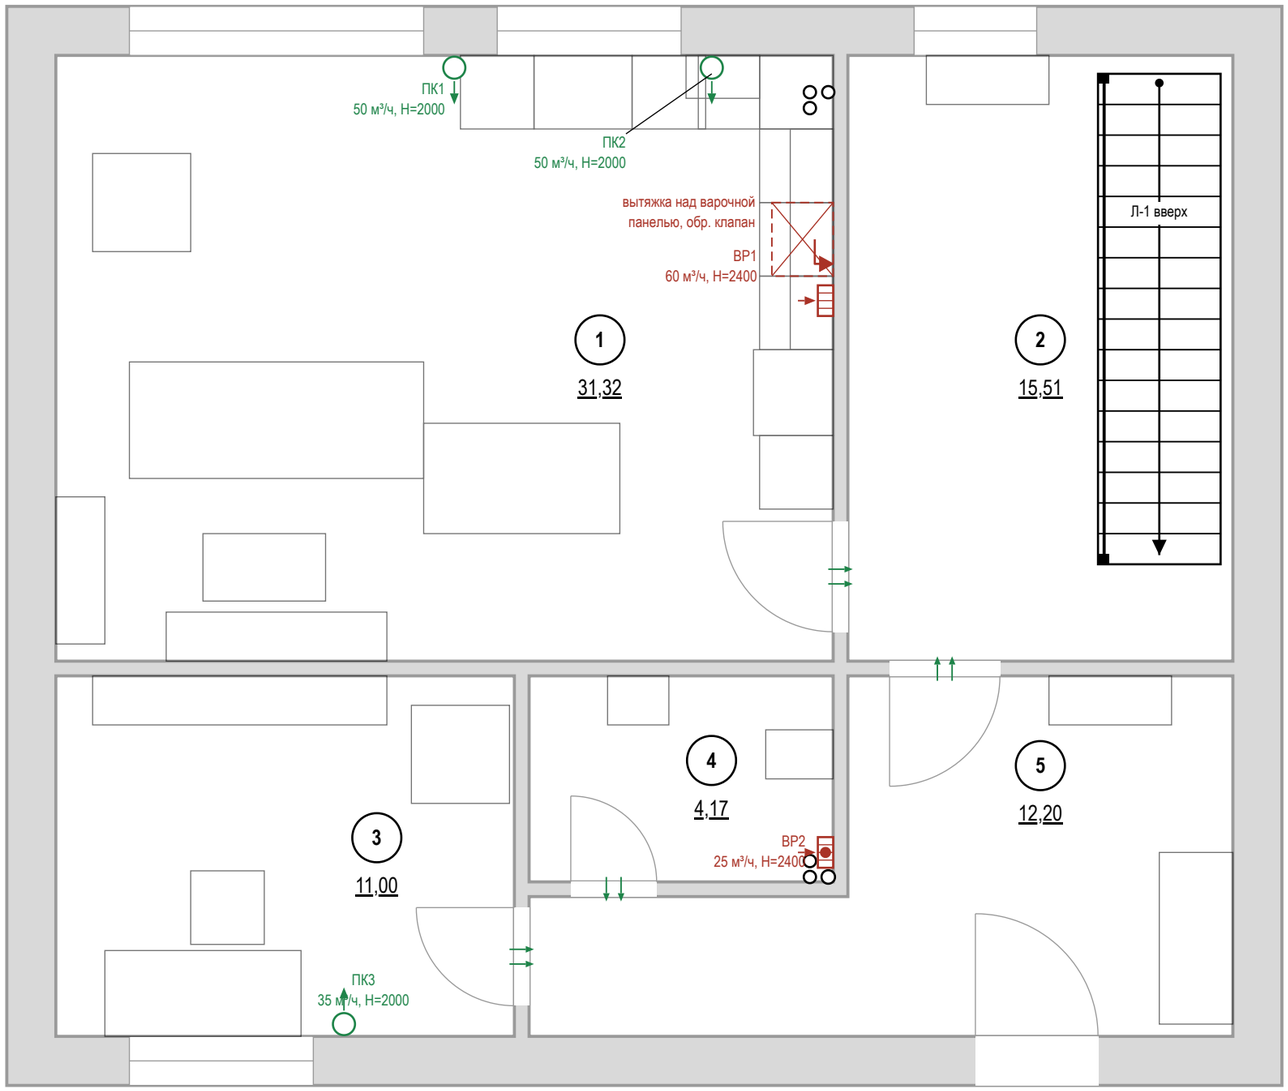

Условные обозначения

- стояк: К1 — канализация, В1 — ХВС, Т3 — ГВС
- номер помещения, площадь м²
- вытяжная решётка в вентканал: марка, расход м³/ч, Н центра от чистого пола
- вытяжная решётка с бытовым вентилятором и обратным клапаном: марка, расход, Н
- приточный клапан (КИВ) в наружной стене: марка, расход, Н центра
- переток: зазор под полотном или переточная решётка
- кухонная вытяжка над варочной панелью
- воздуховод кухонной вытяжки в коробе под потолком
- отдельный вход воздуховода в вентканал, обратный клапан

Воздухообмен, м³/ч

№	Помещение	Выт. норма	Выт. проект	Прит. норма	Прит. проект	Устройства
1	Гостиная-кухня	60	60	94	100	ВР1, ПК1, ПК2
3	Кабинет			33	35	ПК3
4	Санузел гостевой	25	25			ВР2
	Итого	**85**	**85**	**120**	**135**	

Воздухообмен квартиры — по большей из сумм притока и вытяжки: норма 120 м³/ч, проект 135 м³/ч.
Приток больше вытяжки на 50 м³/ч — поднять вытяжку.


Примечания

1. Расчёт систем ОВ и подбор оборудования — проектная организация с допуском СРО; лист даёт места, трассы и привязки.
2. Нормы вытяжки — СП 54.13330.2022 (Изм. 1, 2), табл. 7.1: кухня с электроплитой 60 м³/ч, с газовой 100; ванная и совмещённый санузел 50; уборная 25; гардеробная 0,2 ч⁻¹. Приток в жилые — 3 м³/ч на 1 м² (менее 20 м² общей площади на человека), иначе 30 м³/ч на человека.
3. Венткanалы и шахты не сужать, не переносить и не закрывать; вентилятор и кухонная вытяжка — через обратный клапан, без перекрытия естественной тяги.
4. Проектные расходы — не ниже нормы, вытяжка сведена с притоком вентиляторами мокрых помещений. Клапаны — в простенке у окна, центр 2000 мм, не над кроватью, не ближе 300 мм к стоякам отопления; типоразмер — на расход.
5. Кухонная вытяжка в воздухообмен не включена: воздуховод не менее Ø125 в коробе, вход в канал отдельный.
6. Переток — зазор под полотнами межкомнатных дверей или переточная решётка.
7. Кондиционирование заданием не предусмотрено; при установке трассы фреона и дренажа (не менее 40 мм/м, в К1 через сифон) и питание заложить до черновых работ.
8. Привязки оборудования — по паспортам приобретённых моделей, до черновых работ.

					Проект: Дом 120 м²
	Лист	№ док.	Подпись	Дата	План вентиляции · 1-й этаж
Дизайнер	Кырлан А.С.			19.10.26	

Стадия	Лист	Листов
П	42	128

выпуск 19.10.2026 № 66b2a77b4d · стр. 42 из 128

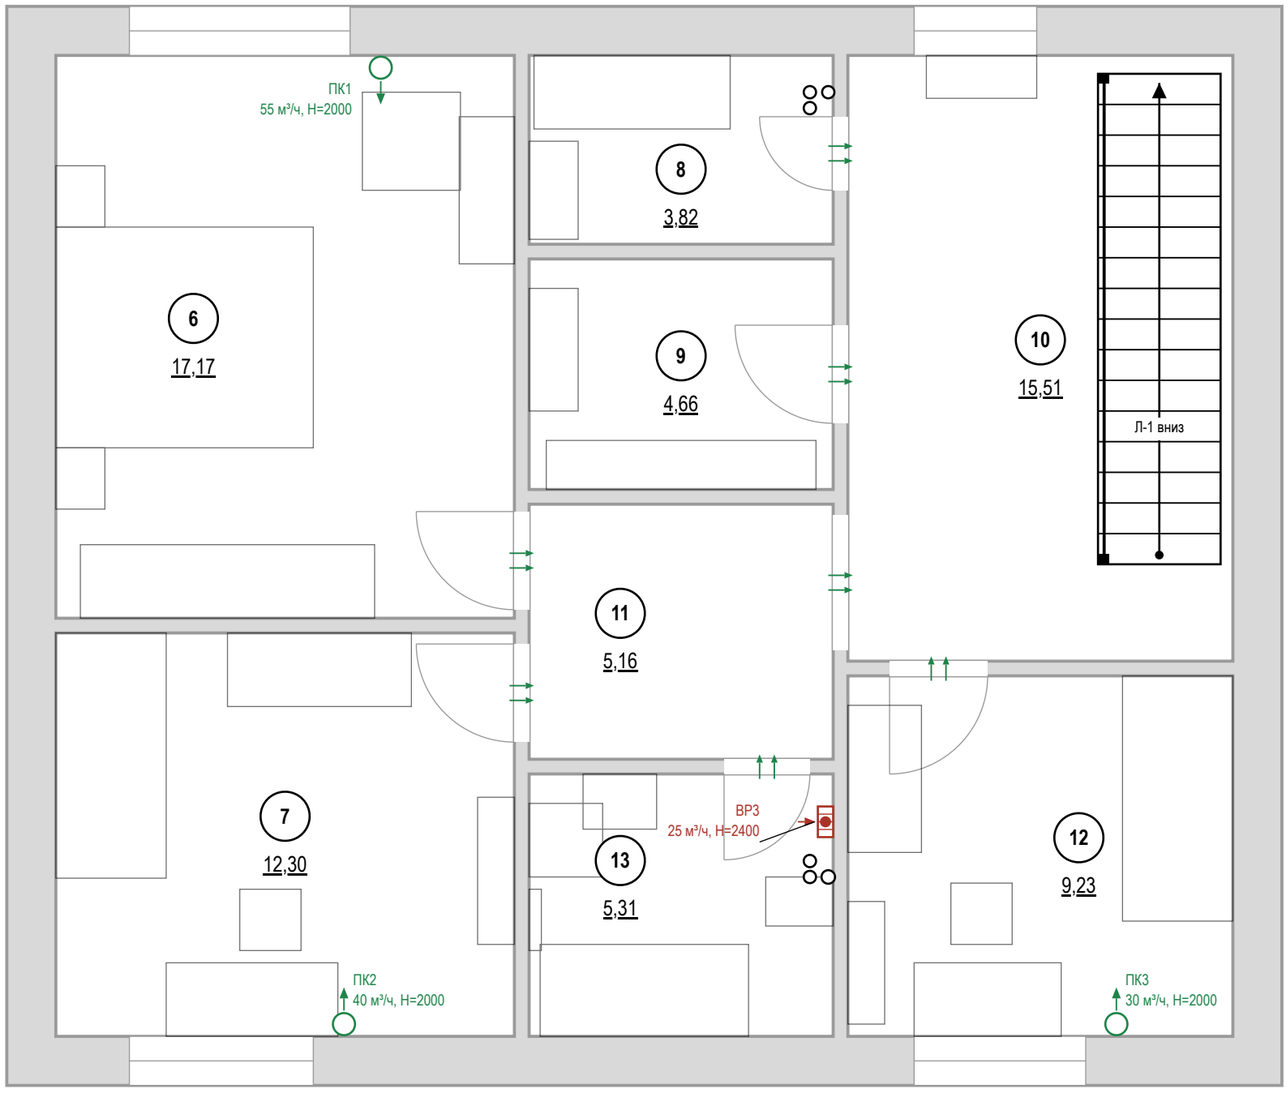

Условные обозначения

- стояк: К1 — канализация, В1 — ХВС, Т3 — ГВС
- 1 — номер помещения, площадь м²
- вытяжная решётка с бытовым вентилятором и обратным клапаном: марка, расход, Н
- приточный клапан (КИВ) в наружной стене: марка, расход, Н центра
- переток: зазор под полотном или переточная решётка

Воздухообмен, м³/ч

№	Помещение	Выт. норма	Выт. проект	Прит. норма	Прит. проект	Устройства
6	Спальня родителей			52	55	ПК1
7	Детская			37	40	ПК2
8	Гардеробная	2				переток
9	Кладовая	3				переток
12	Детская вторая			28	30	ПК3
13	Санузел второго этажа	50	**25 !**			ВР3
	Итого	**55**	**25**	**120**	**125**	


Воздухообмен квартиры — по большей из сумм притока и вытяжки: норма 120 м³/ч, проект 125 м³/ч.
Приток больше вытяжки на 100 м³/ч — поднять вытяжку.
«!» — проект ниже нормы.

Примечания

1. Расчёт систем ОВ и подбор оборудования — проектная организация с допуском СРО; лист даёт места, трассы и привязки.
2. Нормы вытяжки — СП 54.13330.2022 (Изм. 1, 2), табл. 7.1: кухня с электроплитой 60 м³/ч, с газовой 100; ванная и совмещённый санузел 50; уборная 25; гардеробная 0,2 ч⁻¹. Приток в жилые — 3 м³/ч на 1 м² (менее 20 м² общей площади на человека), иначе 30 м³/ч на человека.
3. Вентканалы и шахты не сужать, не переносить и не закрывать; вентилятор и кухонная вытяжка — через обратный клапан, без перекрытия естественной тяги.
4. Проектные расходы — не ниже нормы, вытяжка сведена с притоком вентиляторами мокрых помещений. Клапаны — в простенке у окна, центр 2000 мм, не над кроватью, не ближе 300 мм к стоякам отопления; типоразмер — на расход.
5. Переток — зазор под полотнами межкомнатных дверей или переточная решётка.
6. Кондиционирование заданием не предусмотрено; при установке трассы фреона и дренажа (не менее 40 мм/м, в К1 через сифон) и питание заложить до черновых работ.
7. Привязки оборудования — по паспортам приобретённых моделей, до черновых работ.

					Проект: Дом 120 м²
	Лист	№ док.	Подпись	Дата	План вентиляции · 2-й этаж
Дизайнер	Кырлан А.С.			19.10.26	Стадия: П; Лист: 43; Листов: 128

выпуск 19.10.2026 № 66b2a77b4d · стр. 43 из 128

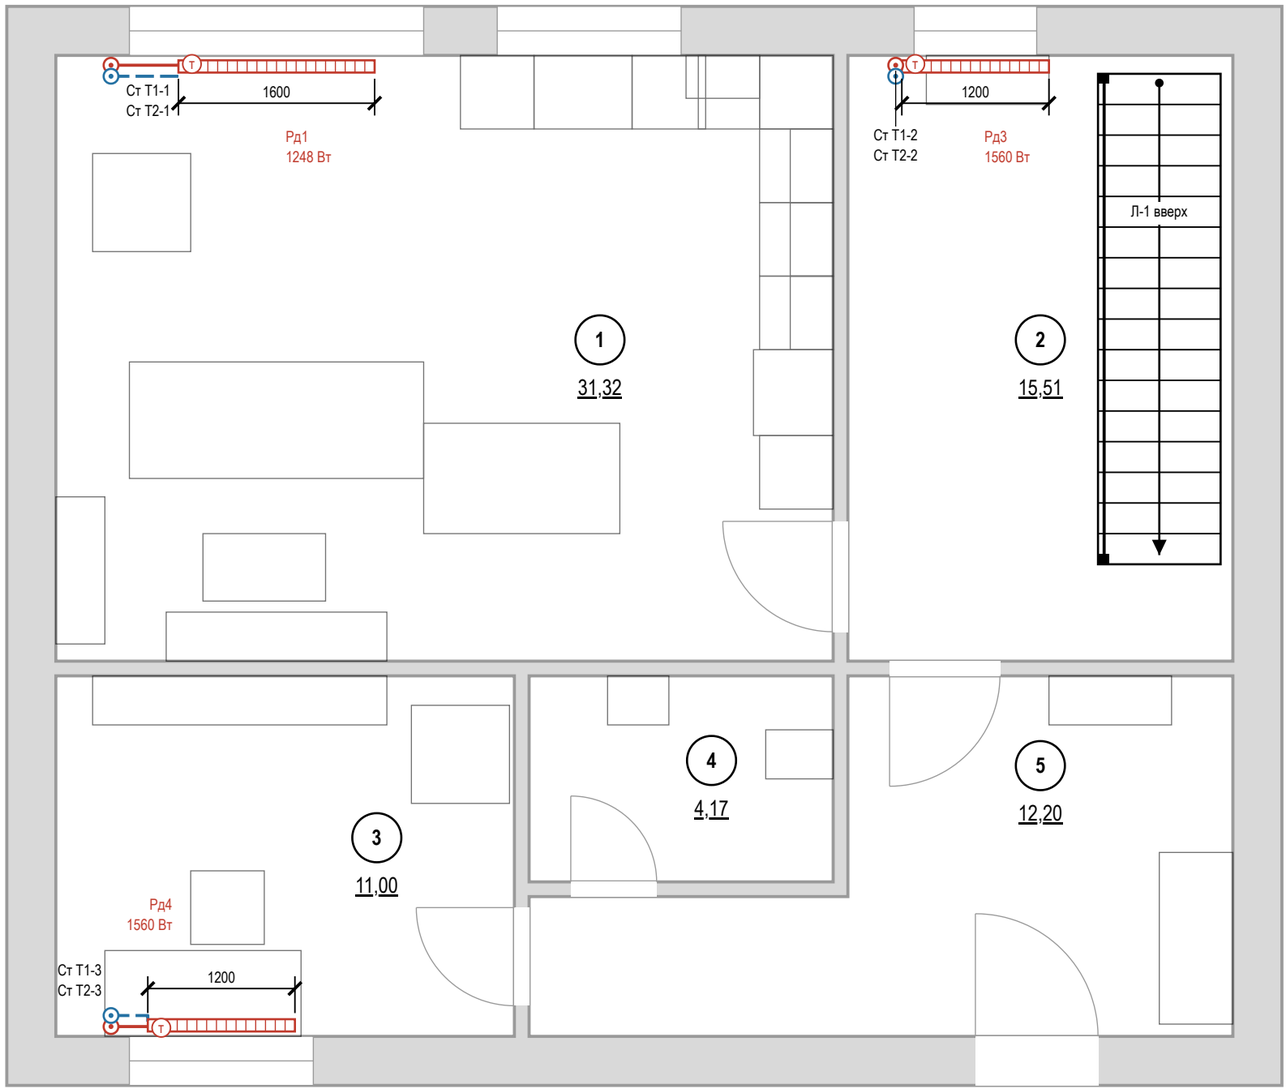

Условные обозначения

- (1) — номер помещения, площадь м²
- радиатор отопления (марка РО-N, длина по плану)
- (Т) — клапан с термоголовкой на подаче
- стояк отопления, подающий (Ст Т1-N)
- стояк отопления, обратный (Ст Т2-N)
- Т1 — отопление, подающий трубопровод
- Т2 — отопление, обратный трубопровод

Ведомость радиаторов

Марка	Помещение	Тип	Д×В×Г, мм	Низ / стена	Q, Вт
Рд1	1. Гостиная-кухня	панельный 22	1600×300×100	100 / 40	1248
Рд3	2. Холл с лестницей	панельный 22	1200×500×100	100 / 40	1560
Рд4	3. Кабинет	панельный 22	1200×500×100	100 / 40	1560

Низ — от чистого пола, стена — зазор до задней панели, мм.


Привязки — до обмера
Стояки отопления в исходных данных не заданы: показаны у откосов окон, подводки — принципиально. До черновых работ — обмер стояков и паспорта приборов; лист перевыпустить по факту.

Примечания

1. Расчёт системы отопления, теплопотерь и подбор приборов — проектная организация с допуском СРО; лист даёт места и привязки.
2. Тип, длина и мощность радиаторов — по теплотехническому расчёту; лист задаёт места, зазоры и подключение.
3. Зазоры радиатора: низ не менее 100 мм от чистого пола, верх не менее 100 мм до подоконника, 30–50 мм от стены до задней панели; центр по оси окна с допуском ±20 мм.
4. Радиаторы не закрывать глухими коробами и мебелью; перенос и замена приборов в многоквартирном доме — переустройство, согласование с управляющей организацией (ЖК РФ ст. 25–26); вынос на лоджию запрещён.
5. Трубы отопления через межквартирные стены не прокладывать (СП 51.13330.2011, п. 9.19); через перекрытия и перегородки — в гильзах.
6. Привязки приборов и подводок — по паспортам приобретённых радиаторов и клапанов, до черновых работ.
7. До закрытия отделкой трубопроводы отопления испытать гидростатическим давлением с оформлением акта (СП 73.13330.2016, 7.2–7.3).

					Проект: Дом 120 м²
	Лист	№ док.	Подпись	Дата	
Дизайнер	Кырлан А.С.			19.10.26	План отопления · 1-й этаж
					Стадия: П; Лист: 44; Листов: 128

выпуск 19.10.2026 № 66b2a77b4d · стр. 44 из 128

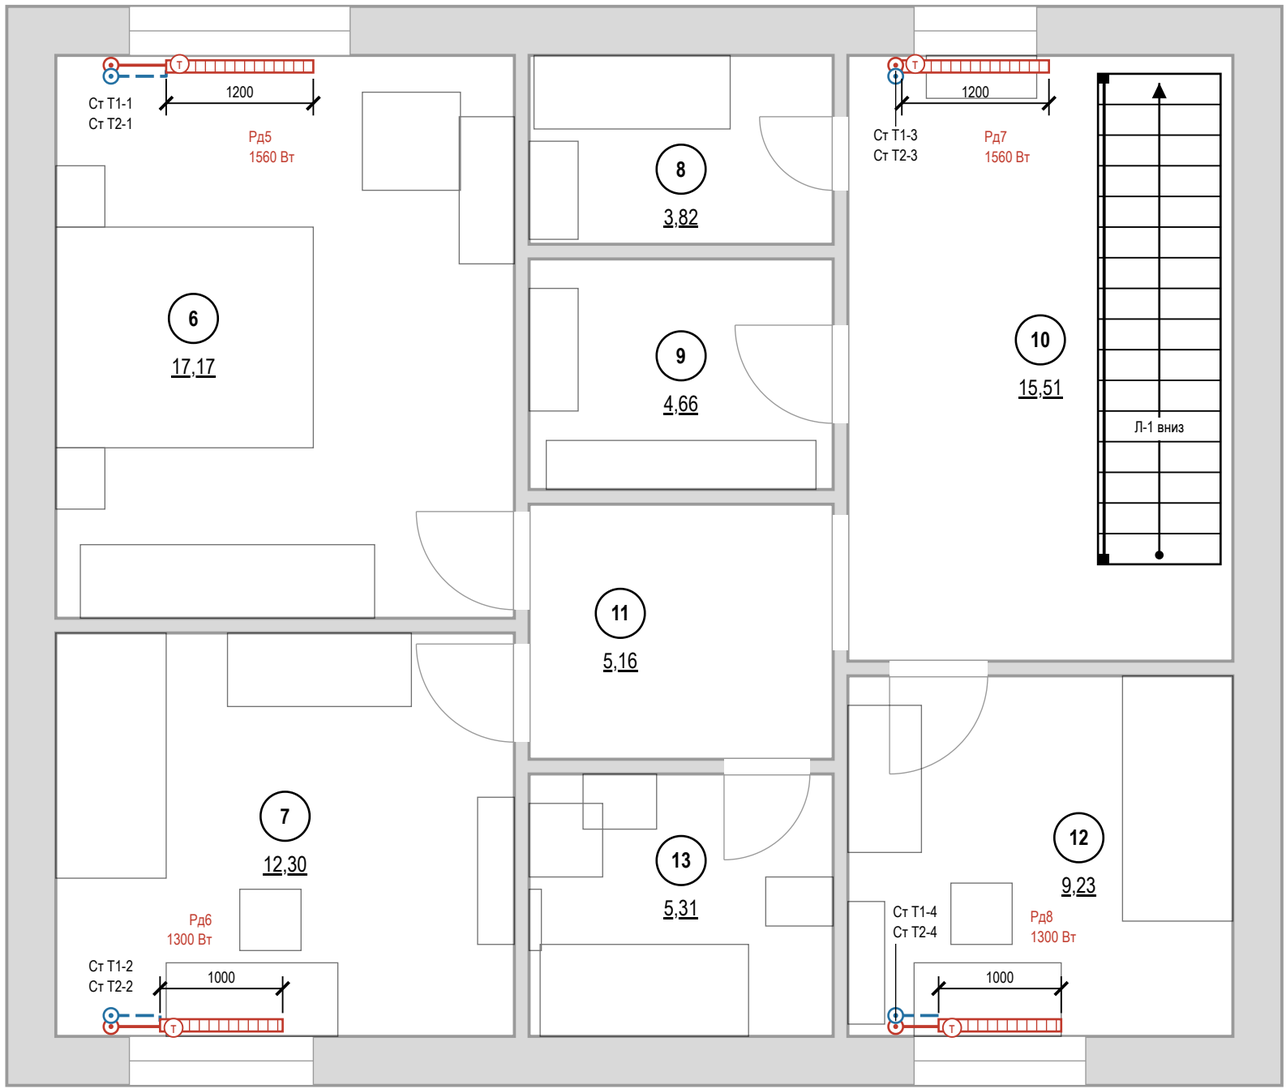

Условные обозначения

- 1 — номер помещения, площадь м²
- радиатор отопления (марка РО-N, длина по плану)
- Т — клапан с термоголовкой на подаче
- стояк отопления, подающий (Ст Т1-N)
- стояк отопления, обратный (Ст Т2-N)
- Т1 — отопление, подающий трубопровод
- Т2 — отопление, обратный трубопровод

Ведомость радиаторов

Марка	Помещение	Тип	Д×В×Г, мм	Низ / стена	Q, Вт
Рд5	6. Спальня родителей	панельный 22	1200×500×100	100 / 40	1560
Рд6	7. Детская	панельный 22	1000×500×100	100 / 40	1300
Рд7	10. Холл второго этажа	панельный 22	1200×500×100	100 / 40	1560
Рд8	12. Детская вторая	панельный 22	1000×500×100	100 / 40	1300

Низ — от чистого пола, стена — зазор до задней панели, мм.

Привязки — до обмера
Стояки отопления в исходных данных не заданы: показаны у откосов окон, подводки — принципиально. До черновых работ — обмер стояков и паспорта приборов; лист перевыпустить по факту.


Примечания

1. Расчёт системы отопления, теплопотерь и подбор приборов — проектная организация с допуском СРО; лист даёт места и привязки.
2. Тип, длина и мощность радиаторов — по теплотехническому расчёту; лист задаёт места, зазоры и подключение.
3. Зазоры радиатора: низ не менее 100 мм от чистого пола, верх не менее 100 мм до подоконника, 30–50 мм от стены до задней панели; центр по оси окна с допуском ±20 мм.
4. Радиаторы не закрывать глухими коробами и мебелью; перенос и замена приборов в многоквартирном доме — переустройство, согласование с управляющей организацией (ЖК РФ ст. 25–26); вынос на лоджию запрещён.
5. Трубы отопления через межквартирные стены не прокладывать (СП 51.13330.2011, п. 9.19); через перекрытия и перегородки — в гильзах.
6. Привязки приборов и подводок — по паспортам приобретённых радиаторов и клапанов, до черновых работ.
7. До закрытия отделкой трубопроводы отопления испытать гидростатическим давлением с оформлением акта (СП 73.13330.2016, 7.2–7.3).




					Проект: Дом 120 м²
	Лист	№ док.	Подпись	Дата	
Дизайнер	Кырлан А.С.			19.10.26	План отопления · 2-й этаж

Стадия	Лист	Листов
П	45	128

выпуск 19.10.2026 № 66b2a77b4d · стр. 45 из 128

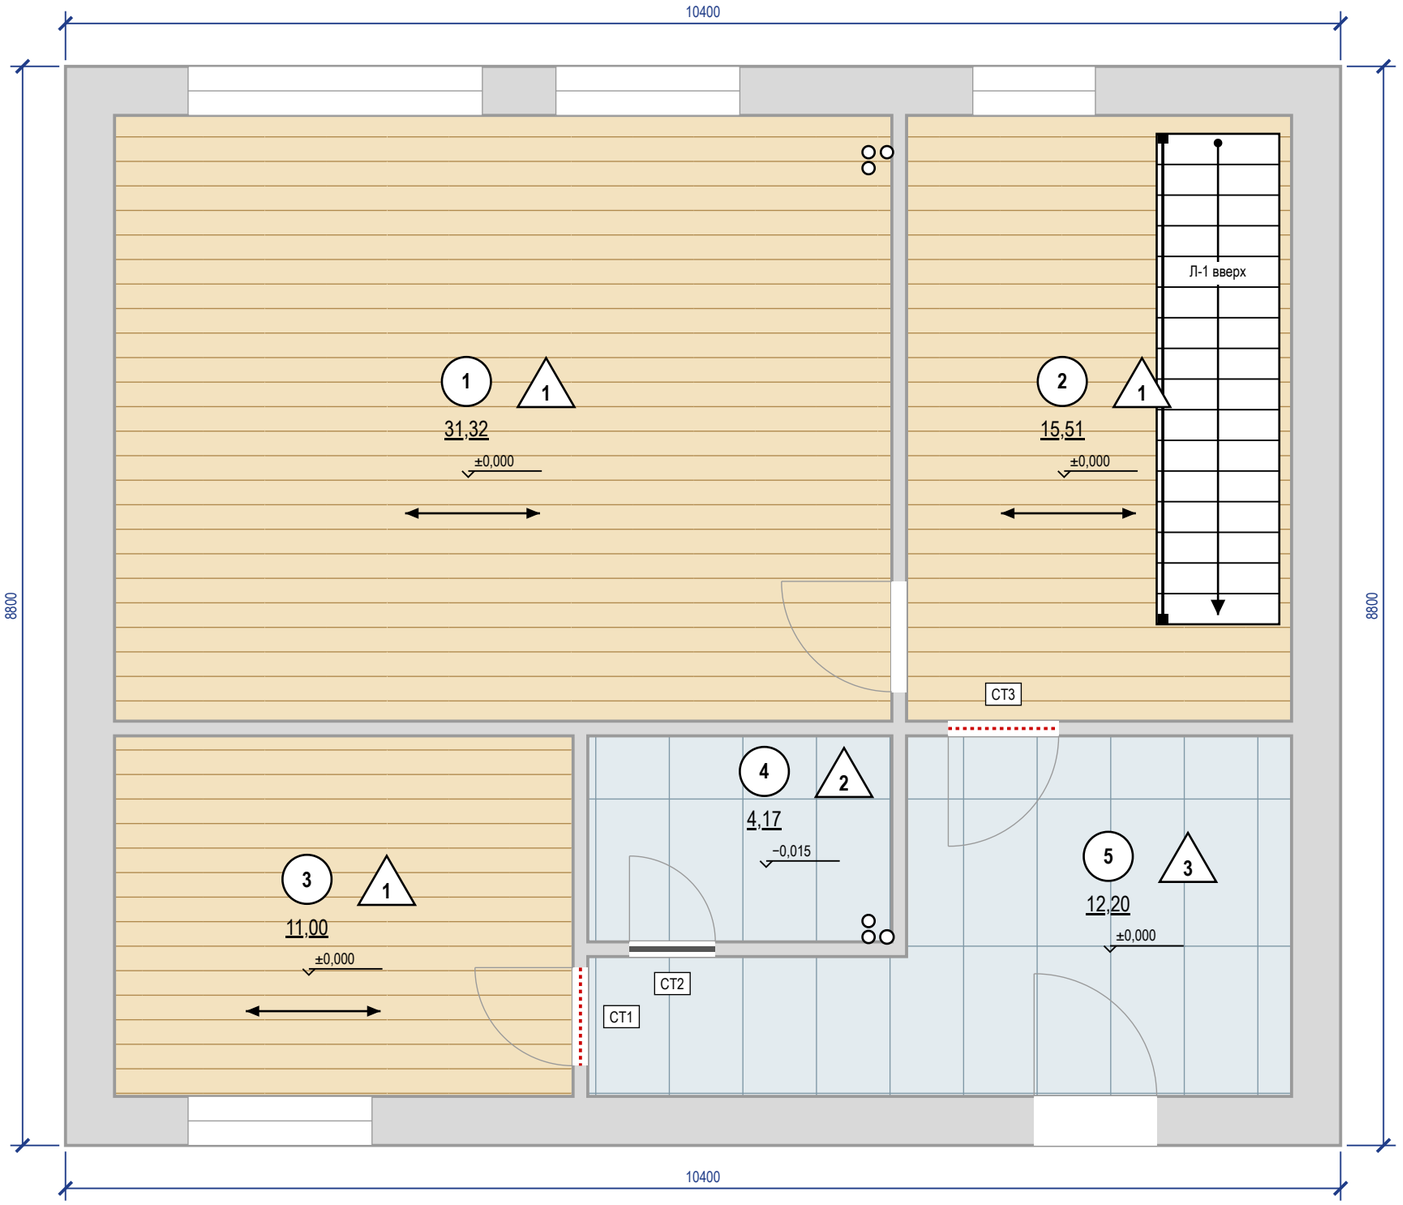

Экспликация полов

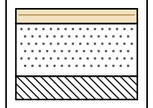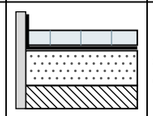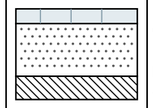Номер помещения	Тип пола	Схема пола	Данные элементов пола (наименование, толщина, основание), мм	Площадь, м²
1, 2, 3	1		Инженерная доска на клею — 14 Стяжка ЦПС М200 — 50 Плита перекрытия Всего 64 мм; ЧП ±0,000, верх плиты −0,064	57,83
4	2		Керамогранит на клею С2 TE S1 — 14 Гидроизоляция обмазочная, 2 слоя, с заведением на стены 200 мм — 2 Стяжка ЦПС М200 — 33 Плита перекрытия Всего 49 мм; ЧП −0,015, верх плиты −0,064	4,17
5	3		Керамогранит на клею С2 TE S1 — 14 Стяжка ЦПС М200 — 50 Плита перекрытия Всего 64 мм; ЧП ±0,000, верх плиты −0,064	12,20
			Итого	**74,20**

Спецификация плинтусов

Наименование	Помещения	Длина, м (с запасом)
Плинтус МДФ под покраску 80×16, крепление к стене, окраска в цвет Tikkurila G503	1, 2, 3, 5	69

Отметки по высоте

±0,000 чистый пол пом. 1–3, 5; отсчёт высот
−0,015 чистый пол пом. 4, ниже на 15 мм
−0,064 верх плиты — расчёт, не замер (задание на обмер)
сущ. пол снимается до плиты; не замерен (задание на обмер)

Примечания

1. За отметку ±0,000 принят чистый пол, не существующий (блок отметок). Площади — по чистым размерам помещений, м²; размеры — в мм.
2. Стык разнотипных покрытий — по оси дверного полотна (под полотном в закрытом положении); решение стыка — по ведомости стыков.
3. Пол санузлов ниже смежных помещений на 15 мм за счёт меньшей толщины стяжки (верх плиты общий — по экспликации полов); гидроизоляция по стяжке с заведением на стены не менее 200 мм (СП 29.13330.2011, п. 7.2), до облицовки — тест проливом и акт скрытых работ.
4. Трубопроводы в конструкции пола не прокладываются: пирог пола 49–64 мм не вмещает выпуски канализации с уклоном — выпуски К1 ведутся по стенам над чистым полом в коробах.
5. Штучные покрытия (инженерная доска): направление — по стрелке; влажность основания по СМ не более 2,0 % (по ТУ изготовителя).
6. Ровность основания — просвет под 2-метровой рейкой не более 2 мм: пом. 1, 2, 3 (инженерная доска), пом. 4, 5 (керамогранит); проверить до укладки покрытия (СП 71.13330.2017, табл. 8.5).
7. Сетка на плитке — условная, в размер формата; точка старта и раскладка — по листу раскладки плитки.
8. Пироги полов — по экспликации полов: слои сверху вниз, толщины в мм; гидроизоляция мокрых зон — в пироге и в ведомости отделки; схема пола — без масштаба.



					Проект: Дом 120 м²
	Лист	№ док.	Подпись	Дата	План покрытий пола · 1-й этаж
Дизайнер	Кырлан А.С.			19.10.26	

Стадия	Лист	Листов
П	46	128

выпуск 19.10.2026 № 66b2a77b4d · стр. 46 из 128



Экспликация полов

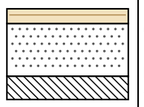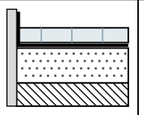Номер помещения	Тип пола	Схема пола	Данные элементов пола (наименование, толщина, основание), мм	Площадь, м²
6, 7, 8, 10, 11, 12	1		Инженерная доска на клею — 14 Стяжка ЦПС М200 — 50 Плита перекрытия Всего 64 мм; ЧП ±0,000, верх плиты −0,064	63,19
9	2		Инженерная доска, 1167-4250, 2100×127 мм, на клею ЧП ±0,000	4,66
13	3		Керамогранит на клею С2 TE S1 — 14 Гидроизоляция обмазочная, 2 слоя, с заведением на стены 200 мм — 2 Стяжка ЦПС М200 — 33 Плита перекрытия Всего 49 мм; ЧП −0,015, верх плиты −0,064	5,31
			Итого	**73,16**

Спецификация плинтусов

Наименование	Помещения	Длина, м (с запасом)
Плинтус МДФ под покраску 80×16, крепление к стене, окраска в цвет Tikkurila G503	6, 8, 10, 11	47
SX165, h = 69 мм, крепление к стене, окраска в цвет Tikkurila G503	7, 9, 12	36

Отметки по высоте

±0,000 чистый пол пом. 6–12; отсчёт высот
−0,015 чистый пол пом. 13, ниже на 15 мм
−0,064 верх плиты — расчёт, не замер (задание на обмер)
сущ. пол снимается до плиты; не замерен (задание на обмер)

Примечания


1. За отметку ±0,000 принят чистый пол, не существующий (блок отметок). Площади — по чистым размерам помещений, м²; размеры — в мм.
2. Стык разнотипных покрытий — по оси дверного полотна (под полотном в закрытом положении); решение стыка — по ведомости стыков.
3. Пол санузлов ниже смежных помещений на 15 мм за счёт меньшей толщины стяжки (верх плиты общий — по экспликации полов); гидроизоляция по стяжке с заведением на стены не менее 200 мм (СП 29.13330.2011, п. 7.2), до облицовки — тест проливом и акт скрытых работ.
4. Трубопроводы в конструкции пола не прокладываются: пирог пола 49–64 мм не вмещает выпуски канализации с уклоном — выпуски К1 ведутся по стенам над чистым полом в коробах.
5. Штучные покрытия (инженерная доска): направление — по стрелке; влажность основания по СМ не более 2,0 % (по ТУ изготовителя).
6. Ровность основания — просвет под 2-метровой рейкой не более 2 мм: пом. 6, 7, 8, 9, 10, 11, 12 (инженерная доска), пом. 13 (керамогранит); проверить до укладки покрытия (СП 71.13330.2017, табл. 8.5).
7. Сетка на плитке — условная, в размер формата; точка старта и раскладка — по листу раскладки плитки.
8. Пироги полов — по экспликации полов: слои сверху вниз, толщины в мм; гидроизоляция мокрых зон — в пироге и в ведомости отделки; схема пола — без масштаба.

					Проект: Дом 120 м²
	Лист	№ док.	Подпись	Дата	План покрытий пола · 2-й этаж
Дизайнер	Кырлан А.С.			19.10.26	


Стадия	Лист	Листов
П	47	128

выпуск 19.10.2026 № 66b2a77b4d · стр. 47 из 128

Фрагмент 1. Санузел гостевой (пом. 4). Пол 600×600, шов 2 мм, М 1:25

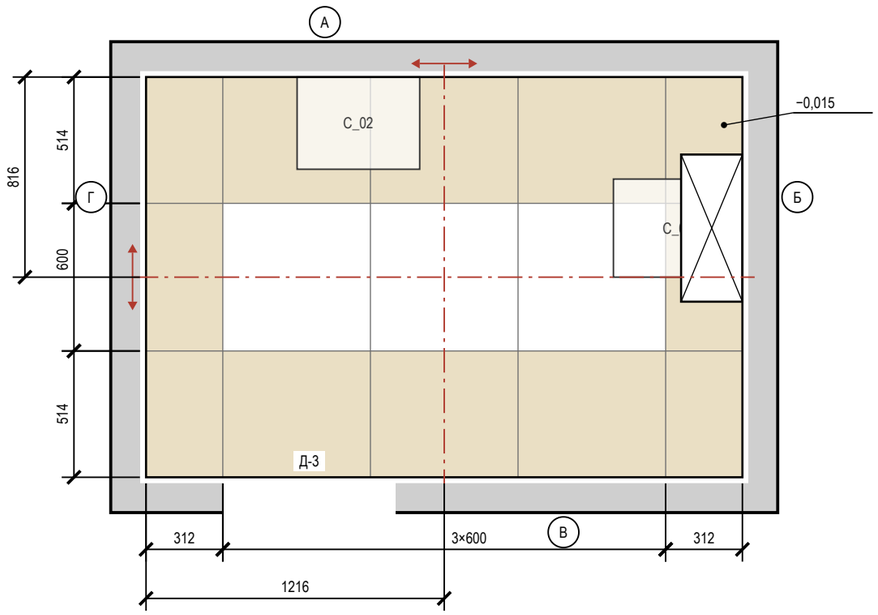

Фрагмент 2. Санузел второго этажа (пом. 13). Пол 600×600, шов 2 мм, М 1:25

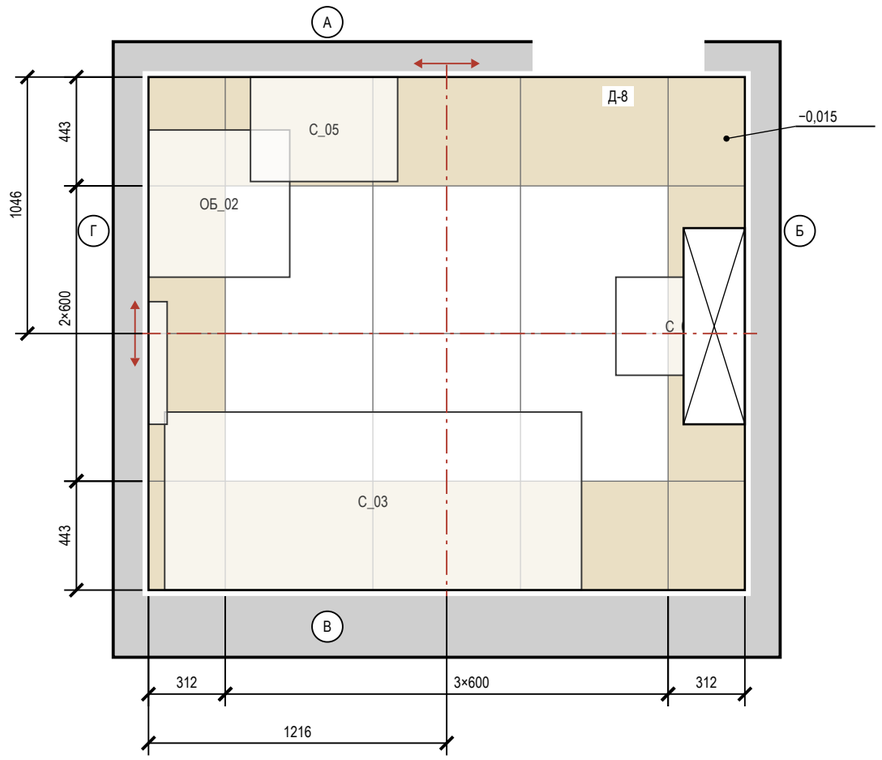

Примечания

1. Раскладка от чистовых размеров: стены санузлов теряют 10 + 5 + 9 = 24 мм на сторону (штукатурка, клей, плитка); подрезки чистые, без шва.
2. Старт — от центра помещения (штрихпунктир, стрелки направление укладки); размер старта — от чистовых стен Г и А.
3. Раскладка пола «Прихожая» и фартука «Гостиная-кухня» и фартука «Гостиная-кухня» — на листе «Раскладка плитки. Прихожая. Фартук кухни».
4. Калибр партии не задан — до укладки замерить (рабочий размер W, ГОСТ 13996-2019) и пересчитать подрезки.
5. Количество: целые по раскладке + по одной на подрезку, запас 10 %; один артикул — одна партия и тон. Исключены поддон, короб, проёмы и места за коробом; S — по чистым граням: стены нетто = зона облицовки по ведомости отделки − место за коробом инсталляции 1,68 м² (плитку за коробом не кладут), короб отдельной строкой.
6. Клей C2 TE S1 Ceresit CM 17; C2 TE S1 (ГОСТ Р 56387-2018), затирка CG2WA Mapei Ultracolor Plus 132; CG2WA; расход — по ТУ выбранной марки.
7. Гидроизоляция: пол и стены 200 мм от ЧП; над ванной — до 2000 и 300 мм за борт (см. развёртки); акт скрытых работ, пролив 24 ч.
8. Швы пола совмещены со швами стены А; по периметру — демпферная лента.
9. Отметка чистого пола −0,015, порог 15 мм; стык с соседним покрытием — по оси полотна двери.

Ведомость плитки

Помещение, поверхность	Плитка, код	Формат	Шов	S, м²	Целых	Подр.	С запасом
Санузел гостевой, пол	аналог: керамогранит под травертин	600×600	2	4,17	3	12	17
Санузел гостевой, стены А–Г	аналог: керамогранит под травертин	600×1200	2	16,68	11	21	36
Санузел гостевой, короб инсталляции	аналог: керамогранит под травертин	600×1200	2	1,47	1	3	5
Санузел второго этажа, пол	аналог: керамогранит под травертин	600×600	2	5,31	6	14	22
Санузел второго этажа, стены А–Г	аналог: керамогранит под травертин	600×1200	2	18,10	16	20	40
Санузел второго этажа, короб инсталляции	аналог: керамогранит под травертин	600×1200	2	1,76	0	6	7
Прихожая, пол	A8UZ	600×1200	2	12,20	4	14	20
Гостиная-кухня, фартук (ст. А)	аналог: керамогранит под травертин, матовый	1200×600	2	0,65	0	3	4
Гостиная-кухня, фартук (ст. Б)	аналог: керамогранит под травертин, матовый	1200×600	2	1,35	0	2	3
Итого 600×600				9,48	9	26	39
Итого 600×1200				**52,21**	**32**	**69**	**115**

Ведомость материалов

Материал	Класс, код	Норма расхода	Кол-во
Затирка	CG2WA Mapei Ultracolor Plus 132	(a+b)/ab·шов·t·1,6	4,1 кг
Затирка	CG2WA	(a+b)/ab·шов·t·1,6	0,9 кг
Клей	C2 TE S1 Ceresit CM 17	1,5 кг/м²·мм, слой 5	402 кг (17 меш.)
Клей	C2 TE S1	1,5 кг/м²·мм, слой 5	92 кг (4 меш.)
Гидроизоляция	обмазочная, 2 слоя: пол, стены по периметру и зоны замачивания	по ТУ	19,6 м²
Демпф. лента	по периметру пола из плитки		27,6 м

Условные обозначения


- плитка целая; тонкая линия — шов
- плитка с подрезкой (размер — на цепочке)
- ось старта; стрелки — направление укладки
- сантехприбор: габарит, высота по практике
- короб инсталляции: плитка пола — до короба
- отметка чистого пола на полке выноски, м
- (А) обозначение стены А–Г (как на развёртках)

					Проект: Дом 120 м²
	Лист	№ док.	Подпись	Дата	Раскладка плитки. Планы полов
Дизайнер	Кырлан А.С.			19.10.26	


Стадия	Лист	Листов
П	48	128

выпуск 19.10.2026 № 66b2a77b4d · стр. 48 из 128


Фрагмент 1. Прихожая (пом. 5). Пол 600×1200, шов 2 мм, М 1:25

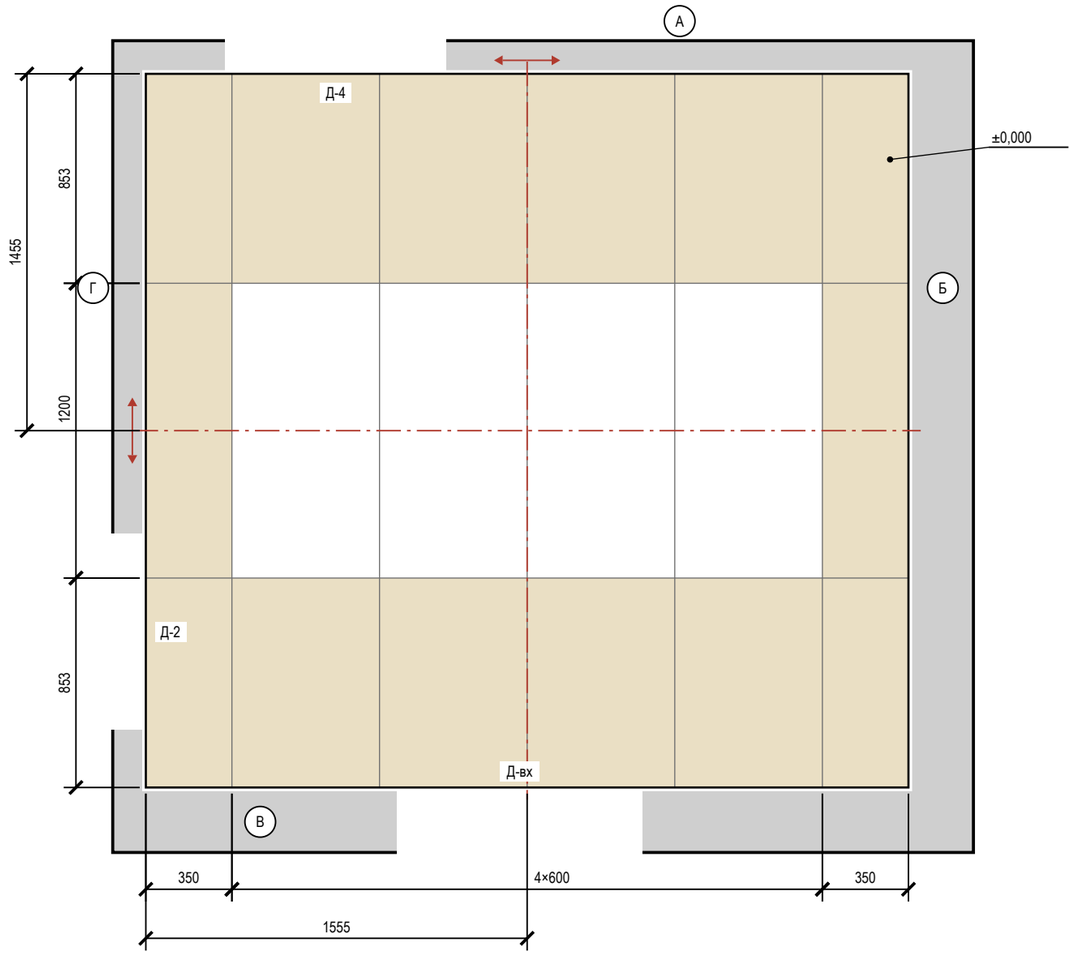

Фрагмент 2. Гостиная-кухня (пом. 1), фартук, стена А. 1200×600, шов 2 мм, М 1:25

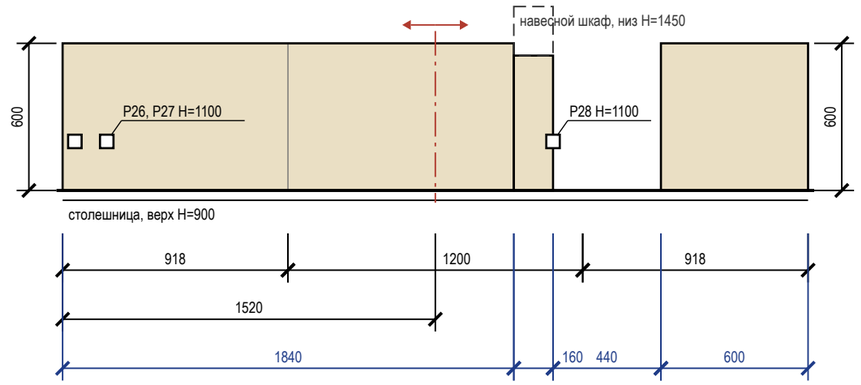

Фрагмент 3. Гостиная-кухня (пом. 1), фартук, стена Б. 1200×600, шов 2 мм, М 1:25

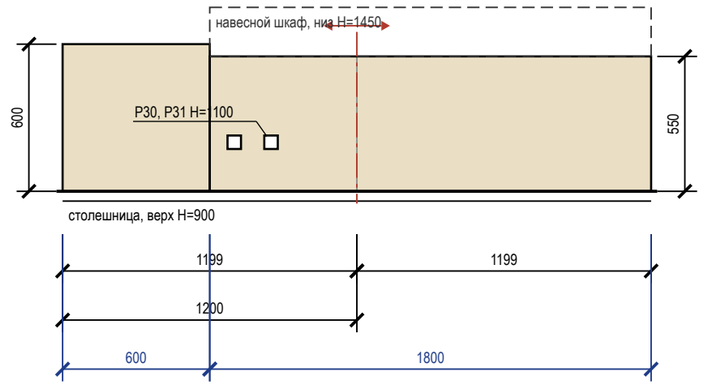

Условные обозначения

- плитка целая; тонкая линия — шов
- плитка с подрезкой (размер — на цепочке)
- ось старта; стрелки — направление укладки
- электроточка: марка и Н — по листам ЭОМ
- столешница (верх)
- навесной шкаф над фартуком
- отметка чистого пола на полке выноски, м
- (А) обозначение стены А–Г (как на развёртках)

Примечания

1. Прихожая: керамогранит 600×1200, длинная сторона — вдоль стен Б и Г, шов 2 мм, прямая раскладка от центра. Стены окрашены: раскладка от чистового контура минус штукатурка и шпаклёвка 15 мм на сторону (принято); подрезки 350 / 853 мм, срез — под плинтус.
2. Прихожая: деформационный зазор по периметру 8–10 мм под плинтусом; в проёмах — стык с соседним покрытием по оси полотна двери. Клей С2 TE S1, затирка CG2WA.
3. Фартук, Гостиная-кухня: 1200×600 горизонтально, шов 2 мм; зоны 1840 мм — 900…1500, 160 мм — 900…1450, 600 мм — 900…1500 (от столешницы до низа навесного шкафа, без шкафа — 600 мм). Старт от центра участка, подрезки 918 мм. Площадь 0,65 м² — как в ведомости отделки.
4. Фартук — после монтажа столешницы, низ на 2–3 мм выше неё, шов со столешницей — санитарный герметик; навесные шкафы — после фартука. Торцы у пенала и стены — профиль или запил 45°.
5. Фартук, Гостиная-кухня: 1200×600 горизонтально, шов 2 мм; зоны 600 мм — 900…1500, 1800 мм — 900…1450 (от столешницы до низа навесного шкафа, без шкафа — 600 мм). Старт от центра участка, подрезки нет мм. Площадь 1,35 м² — как в ведомости отделки.
6. Фартук — после монтажа столешницы, низ на 2–3 мм выше неё, шов со столешницей — санитарный герметик; навесные шкафы — после фартука. Торцы у пенала и стены — профиль или запил 45°.
7. Розетки из таблицы переносятся до черновой электрики: по высоте — на ось ряда плитки, от вертикального шва крупной плитки — не ближе 60 мм. Привязка — от левого края фартука на развёртке.
8. Клей, затирка и итог по форматам — в ведомостях листа «Раскладка плитки. Планы полов».

Подсчёт плитки

Поверхность	Формат	S, м²	Целых	Подр.	С запасом
Прихожая, пол	600×1200	12,20	4	14	20
Гостиная-кухня, фартук (ст. А)	1200×600	0,65	0	3	4
Гостиная-кухня, фартук (ст. Б)	1200×600	1,35	0	2	3

Сдвиг розеток фартука под раскладку

Точка (ЭОМ)	Проект: от угла / Н	Под раскладку: от угла / Н	Сдвиг, мм
Р26, Р27	50, 180 / 1100	50, 180 / 1200	Н +100 — ось ряда
Р28	2000 / 1100	2000 / 1175	Н +75 — ось ряда
Р30, Р31	700, 850 / 1100	700, 850 / 1175	Н +75 — ось ряда

					Проект: Дом 120 м²
	Лист	№ док.	Подпись	Дата	
Дизайнер	Кырлан А.С.			19.10.26	Раскладка плитки. Прихожая. Фартук кухни

Стадия	Лист	Листов
П	49	128

выпуск 19.10.2026 № 66b2a77b4d · стр. 49 из 128



					Проект: Дом 120 м²	
	Лист	№ док.	Подпись	Дата	Визуализация. Вид сверху	Стадия / Лист / Листов
Дизайнер	Кырлан А.С.			19.10.26		П / 50 / 128

выпуск 19.10.2026 66b2a77b4d · стр. 50 из 128



					Проект: Дом 120 м²
	Лист	№ док.	Подпись	Дата	Визуализация. Вид сверху
Дизайнер	Кырлан А.С.			19.10.26	

Стадия	Лист	Листов
П	51	128

выпуск 19.10.2026 № 66b2a77b4d · стр. 51 из 128



					Проект: Дом 120 м²
	Лист	№ док.	Подпись	Дата	Визуализация: Гостиная-кухня
Дизайнер	Кырлан А.С.			19.10.26	

Стадия	Лист	Листов
П	52	128

выпуск 19.10.2026 № 66b2a77b4d · стр. 52 из 128



					Проект: Дом 120 м²	
	Лист	№ док.	Подпись	Дата	Визуализация: Гостиная-кухня	Стадия / Лист / Листов
Дизайнер	Кырлан А.С.			19.10.26		П / 53 / 128

выпуск 19.10.2026 № 66b2a77b4d · стр. 53 из 128



					Проект: Дом 120 м²
	Лист	№ док.	Подпись	Дата	Визуализация: Гостиная-кухня
Дизайнер	Кырлан А.С.			19.10.26	

Стадия	Лист	Листов
П	54	128

выпуск 19.10.2026 № 66b2a77b4d · стр. 54 из 128

Развёртка стены А


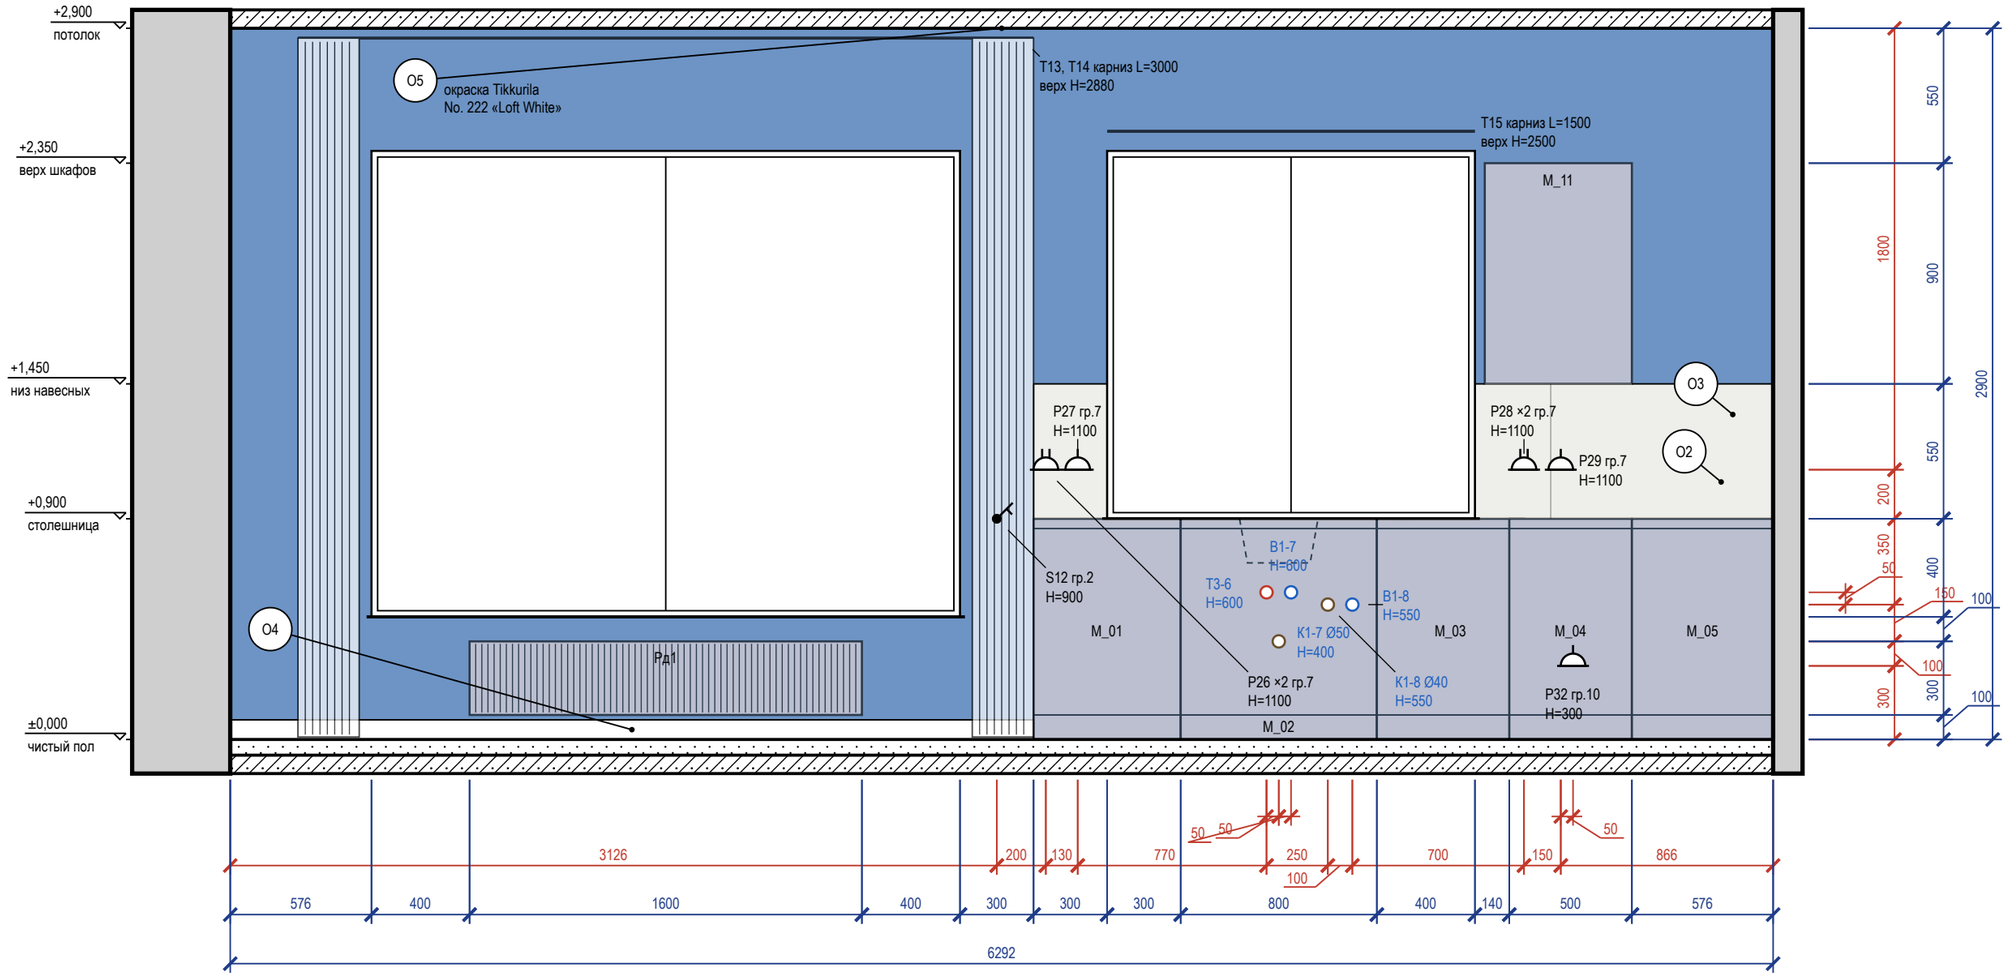


Схема развёрток (М 1:100)

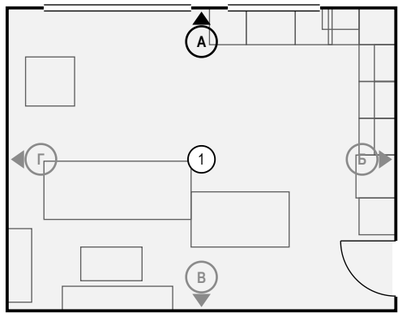

Ведомость отделки (на листе)

Марка	Поверхность	Материал, изделие	Цвет, код	Кол.
O2	фартук	керамогранит, 1200×600×9 мм, аналог: керамогранит под травертин, матовый, затирка CG2WA		0,8 м²
O3	акцентная стена	окраска, Farrow & Ball Modern Emulsion, матовая, подготовка Q3	NCS S 3050-R80B «Эгейский синий»	9,8 м²
O4	плинтус	плинтус МДФ, h 80 мм, аналог: плинтус МДФ под покраску 80×16	Tikkurila G503 «Calla»	3,3 м
O5	потолок	окраска, Tikkurila Anti-Reflex 2, глубокоматовая, подготовка Q3	Little Greene No. 222 «Loft White»	31,3 м²

Визуализация этой стены — лист 52



Примечания

1. Размеры — в мм от чистовых поверхностей стен; условные обозначения и общие указания — лист 2.
2. Выводы ВК — коды и высоты по листу выводов сантехники.
3. Карнизы (шины) — по ведомости текстиля декоратора; длина L и верх H — по развёртке, крепление — до окраски потолка.
4. Выводы кухонной техники — по утверждённому проекту кухни: привязки выводов даются от осей модулей гарнитура.

					Проект: Дом 120 м²
	Лист	№ док.	Подпись	Дата	Развёртка стены А. Гостиная-кухня (пом. 1), кухонный фронт
Дизайнер	Кырлан А.С.			19.10.26	

Стадия	Лист	Листов
П	55	128

выпуск 19.10.2026 № 66b2a77b4d · стр. 55 из 128

Развёртка стены Б


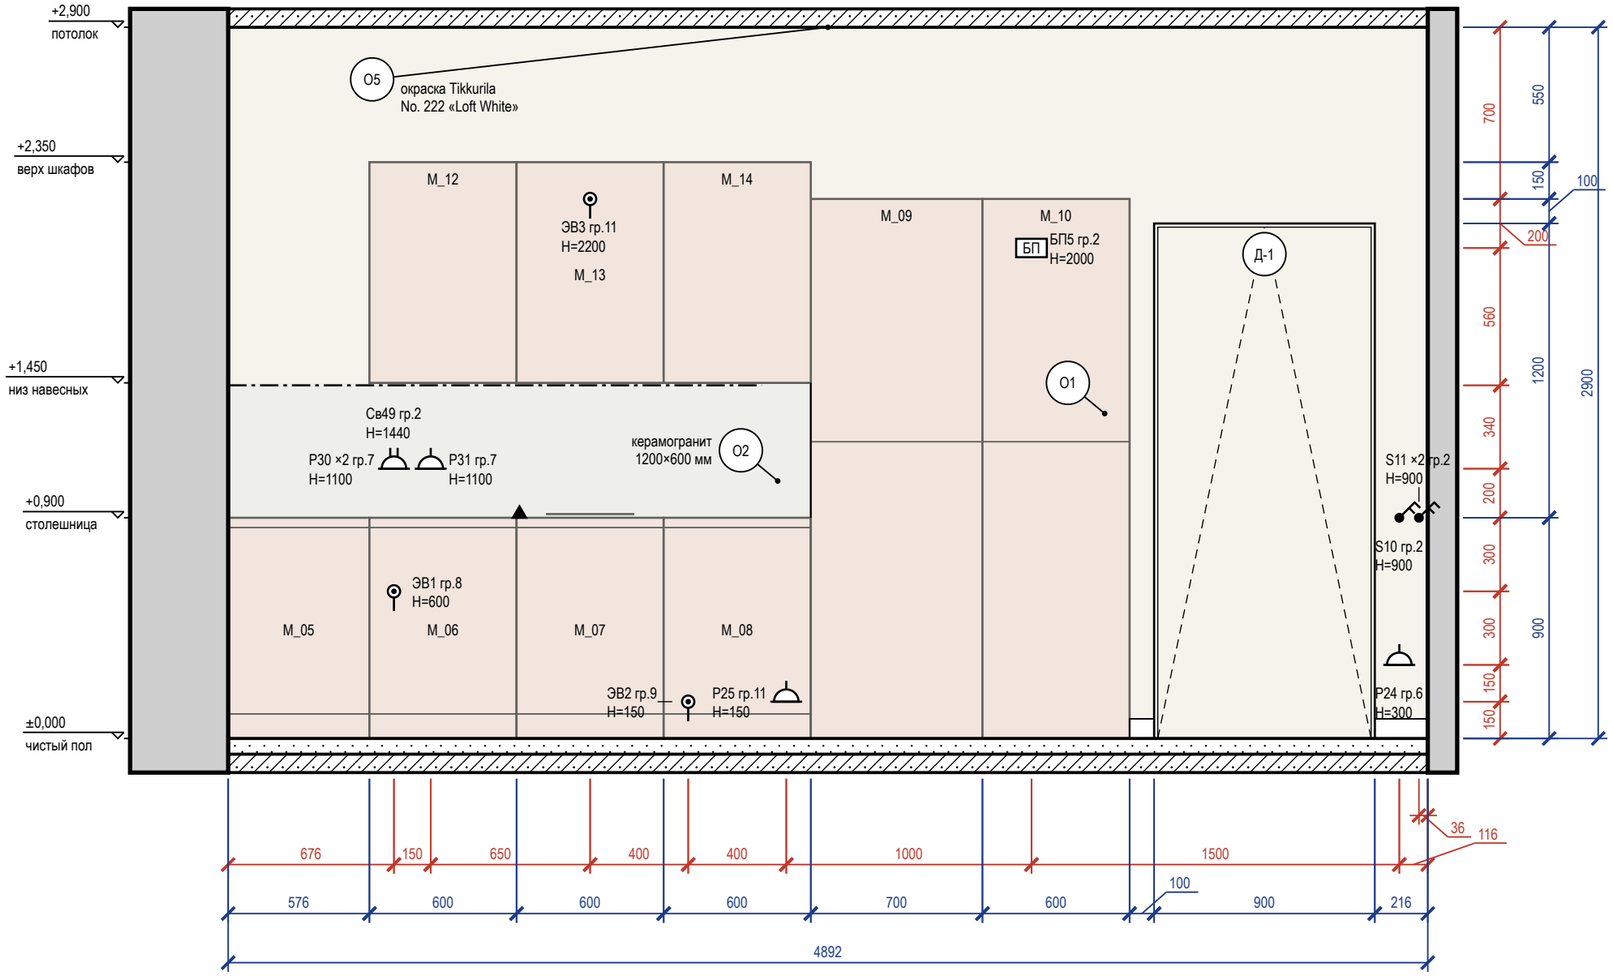


Схема развёрток (М 1:100)

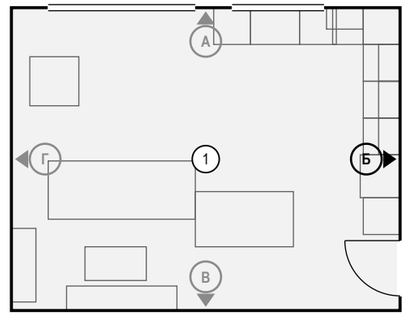

Ведомость отделки (на листе)

Марка	Поверхность	Материал, изделие	Цвет, код	Кол.
О1	стены	окраска, Farrow & Ball Modern Emulsion, матовая, подготовка Q3	Tikkurila G503 «Calla»	11 м²
О2	фартук	керамогранит, 1200×600×9 мм, аналог: керамогранит под травертин, матовый, затирка CG2WA		1,3 м²
О4	плинтус	плинтус МДФ, h 80 мм, аналог: плинтус МДФ под покраску 80×16	Tikkurila G503 «Calla»	0,3 м
О5	потолок	окраска, Tikkurila Anti-Reflex 2, глубокоматовая, подготовка Q3	Little Greene No. 222 «Loft White»	31,3 м²

Визуализация этой стены — лист 53



Примечания

1. Размеры — в мм от чистовых поверхностей стен; условные обозначения и общие указания — лист 2.
2. Двери скрытого монтажа — полотно в плоскости стены, отделка стены по полотну, плинтус прерывается у короба (узел — на листе узлов).
3. Выводы кухонной техники — по утверждённому проекту кухни: привязки выводов даются от осей модулей гарнитура.

					Проект: Дом 120 м²
	Лист	№ док.	Подпись	Дата	Развёртка стены Б. Гостиная-кухня (пом. 1), кухонный фронт
Дизайнер	Кырлан А.С.			19.10.26	

Стадия	Лист	Листов
П	56	128

выпуск 19.10.2026 № 66b2a77b4d · стр. 56 из 128

Развёртка стены В


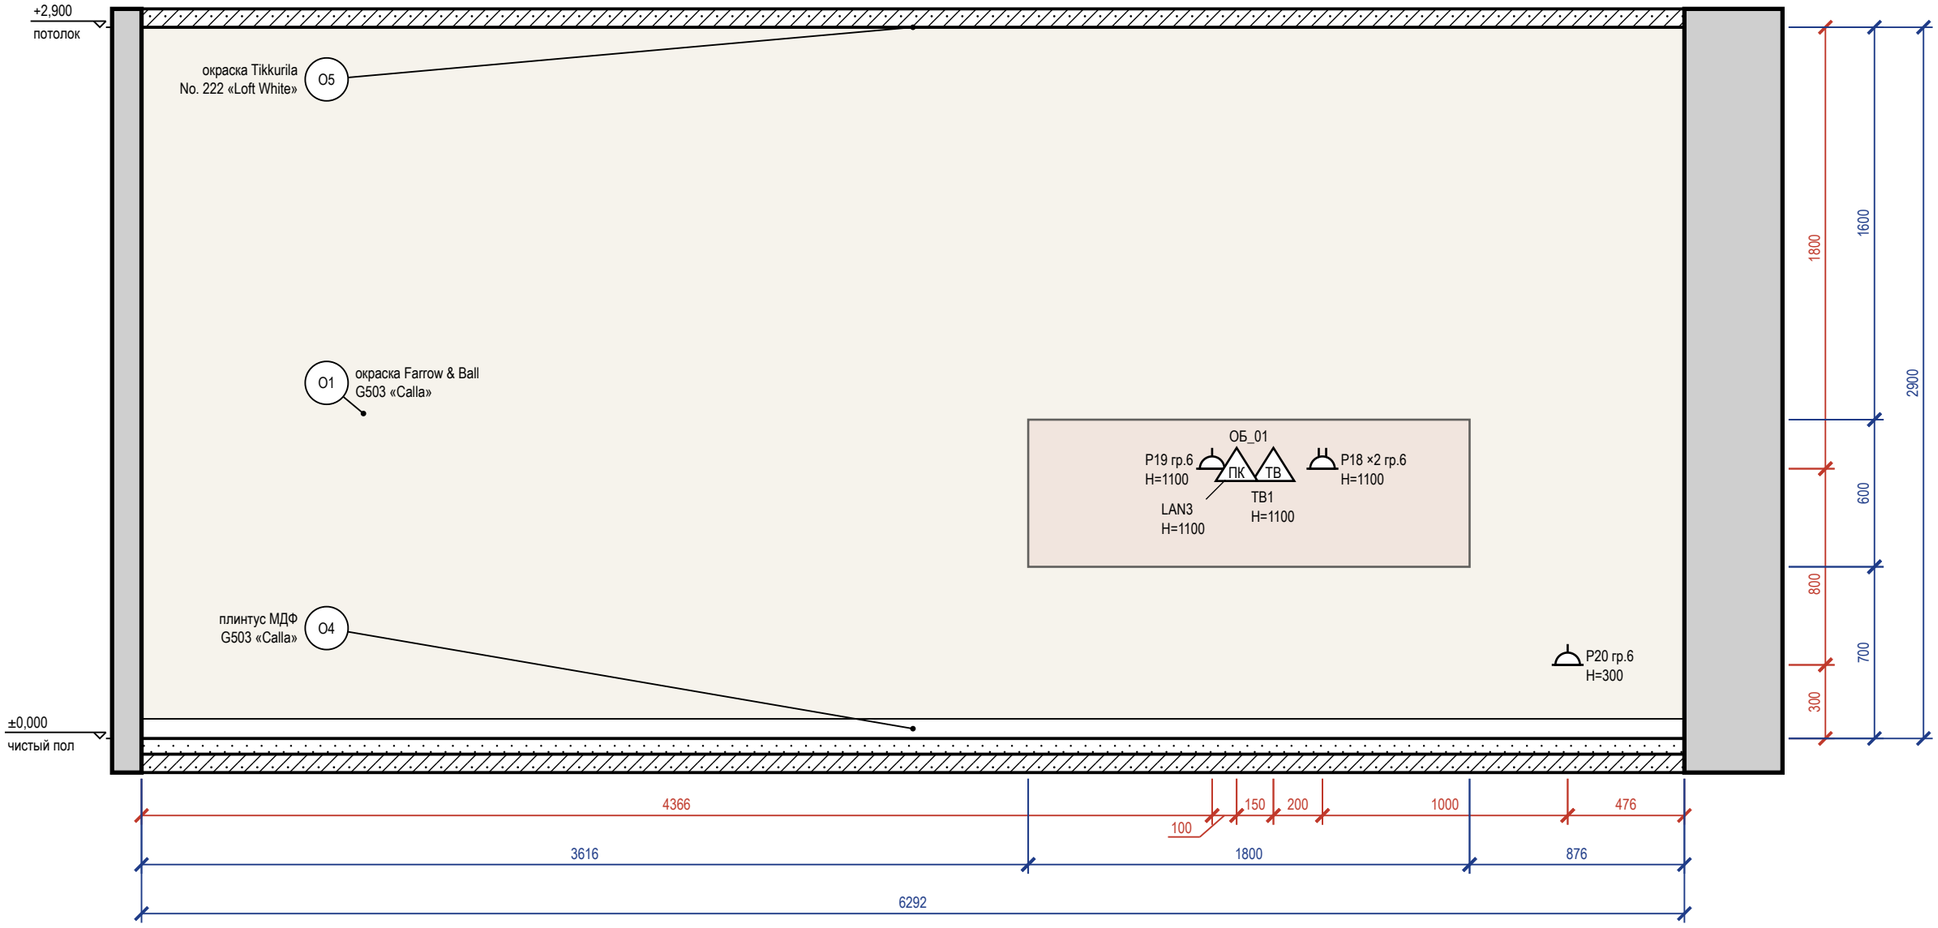


Схема развёрток (М 1:100)

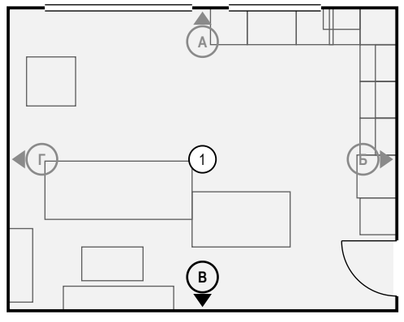

Ведомость отделки (на листе)

Марка	Поверхность	Материал, изделие	Цвет, код	Кол.
О1	стены	окраска, Farrow & Ball Modern Emulsion, матовая, подготовка Q3	Tikkurila G503 «Calla»	18,2 м²
О4	плинтус	плинтус МДФ, h 80 мм, аналог: плинтус МДФ под покраску 80×16	Tikkurila G503 «Calla»	6,3 м
О5	потолок	окраска, Tikkurila Anti-Reflex 2, глубокоматовая, подготовка Q3	Little Greene No. 222 «Loft White»	31,3 м²

Визуализация этой стены — лист 54



Примечания

1. Размеры — в мм от чистовых поверхностей стен; условные обозначения и общие указания — лист 2.
2. Схема мебели, приборов и декора не является технической документацией для производства мебели; габариты — по паспортам изделий.

					Проект: Дом 120 м²
	Лист	№ док.	Подпись	Дата	Развёртка стены В. Гостиная-кухня (пом. 1)
Дизайнер	Кырлан А.С.			19.10.26	

Стадия	Лист	Листов
П	57	128

выпуск 19.10.2026 № 66b2a77b4d · стр. 57 из 128

Развёртка стены Г


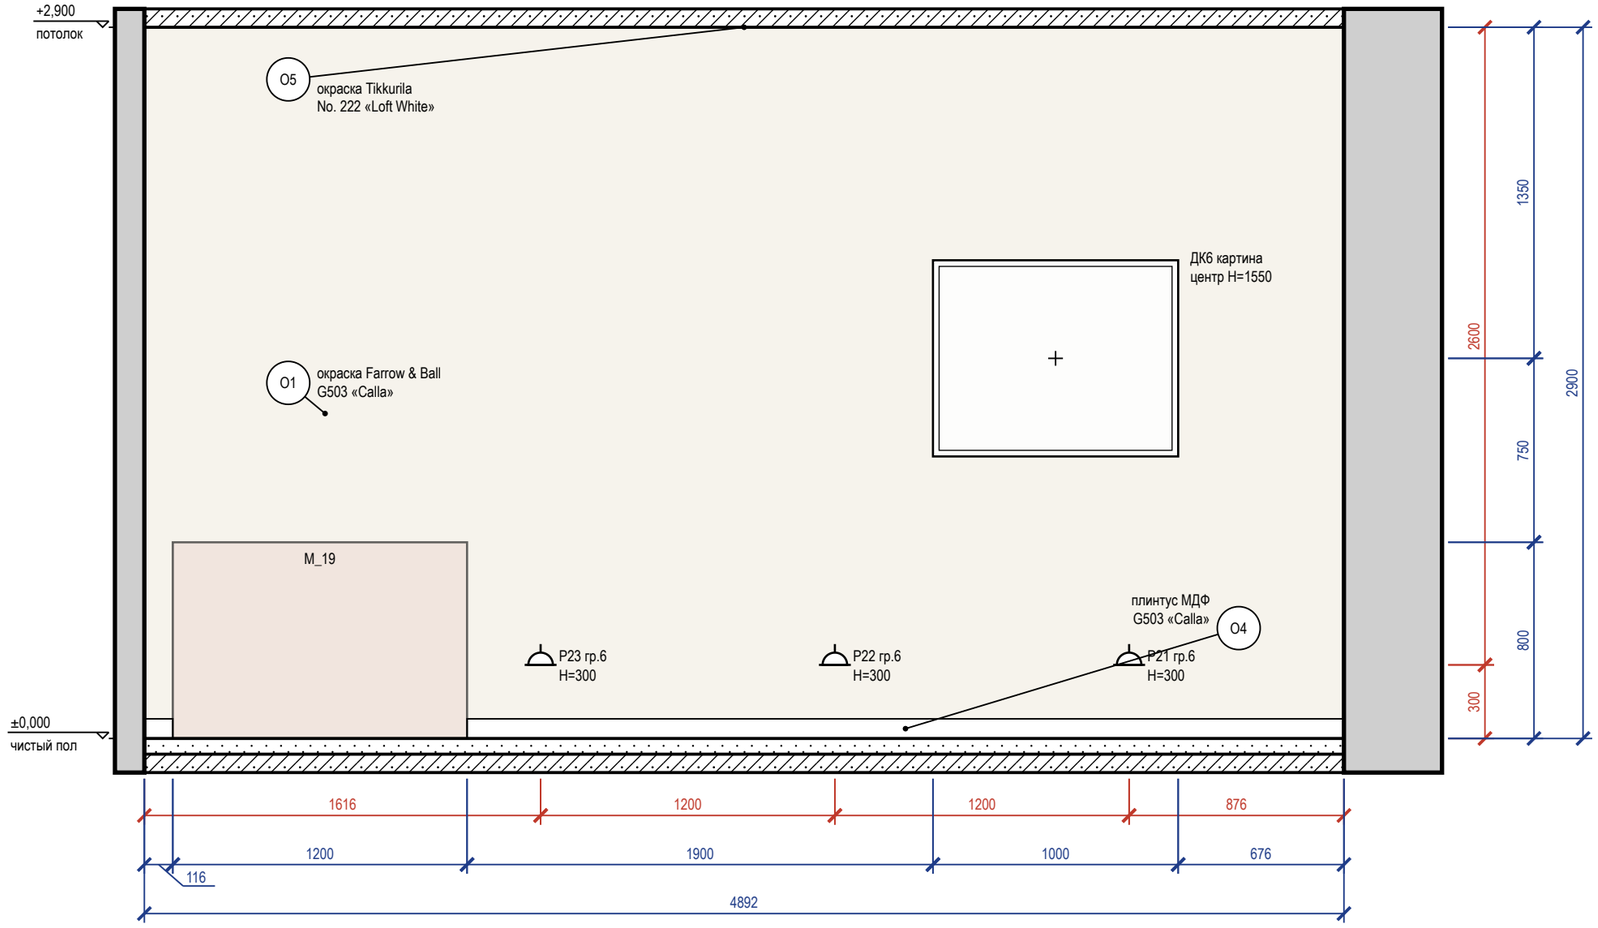


Схема развёрток (М 1:100)

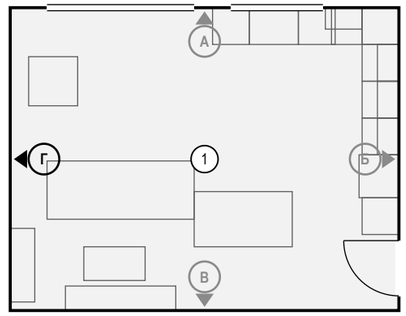

Ведомость отделки (на листе)

Марка	Поверхность	Материал, изделие	Цвет, код	Кол.
О1	стены	окраска, Farrow & Ball Modern Emulsion, матовая, подготовка Q3	Tikkurila G503 «Calla»	14,2 м²
О4	плинтус	плинтус МДФ, h 80 мм, аналог: плинтус МДФ под покраску 80×16	Tikkurila G503 «Calla»	3,7 м
О5	потолок	окраска, Tikkurila Anti-Reflex 2, глубокоматовая, подготовка Q3	Little Greene No. 222 «Loft White»	31,3 м²

Визуализация этой стены



Примечания

1. Размеры — в мм от чистовых поверхностей стен; условные обозначения и общие указания — лист 2.
2. Картины и зеркала крепить к основанию по паспорту изделия (закладные и анкеры — в перечне скрытых работ); крест — ось центра предмета.

					Проект: Дом 120 м²
	Лист	№ док.	Подпись	Дата	Развёртка стены Г. Гостиная-кухня (пом. 1)
Дизайнер	Кырлан А.С.			19.10.26	

Стадия	Лист	Листов
П	58	128

выпуск 19.10.2026 № 66b2a77b4d · стр. 58 из 128



					Проект: Дом 120 м²
	Лист	№ док.	Подпись	Дата	
Дизайнер	Кырлан А.С.			19.10.26	Визуализация: Холл с лестницей

Стадия	Лист	Листов
П	59	128

выпуск 19.10.2026 № 66b2a77b4d · стр. 59 из 128

Развёртка стены А


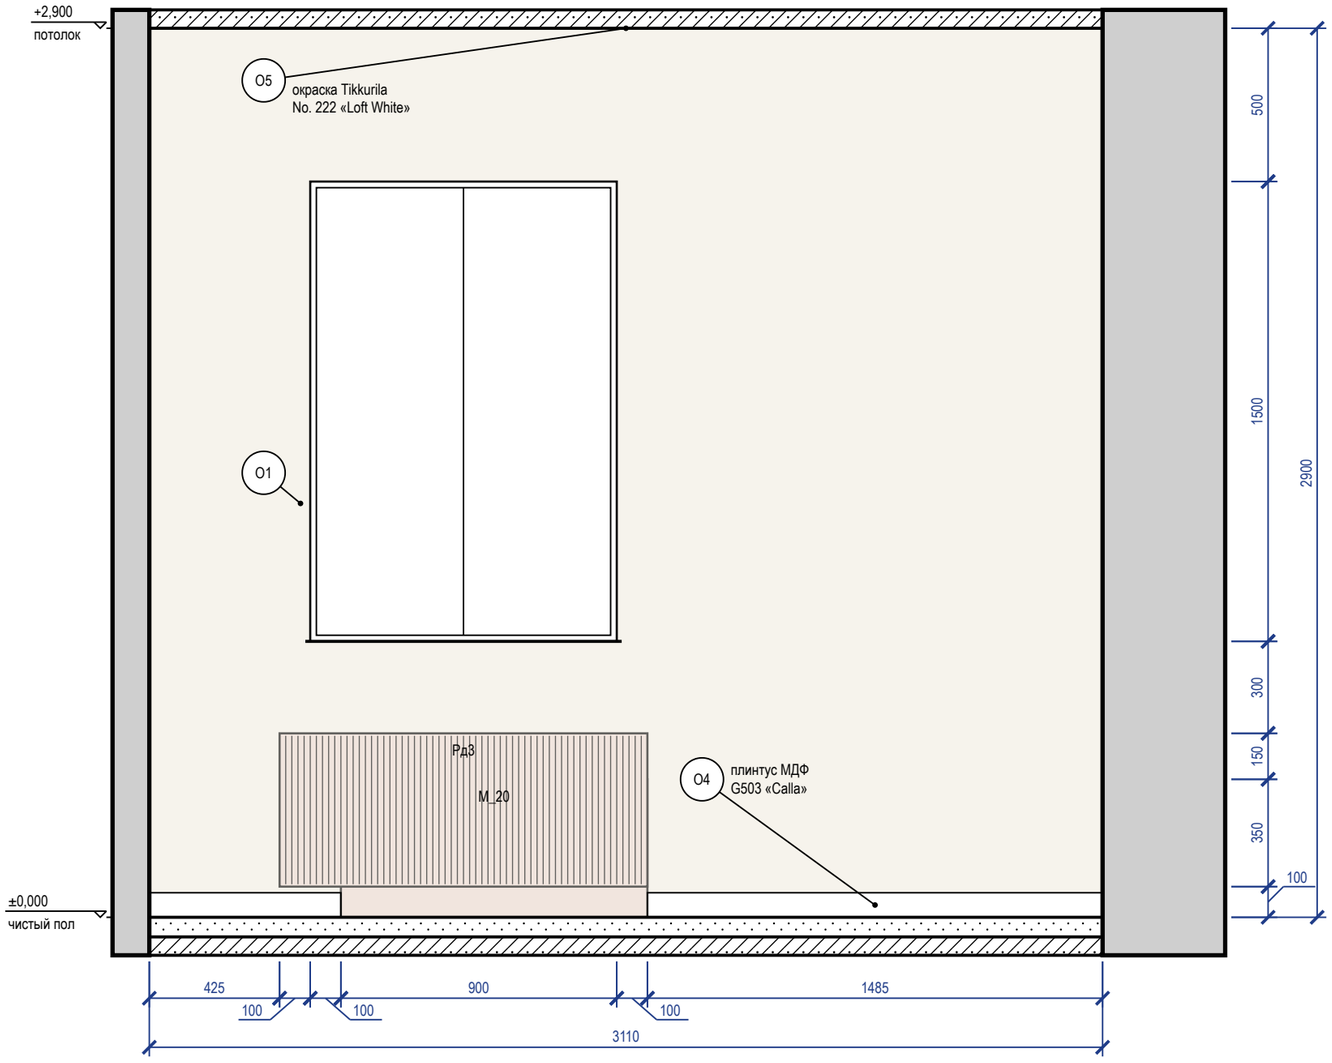


Схема развёрток (М 1:100)

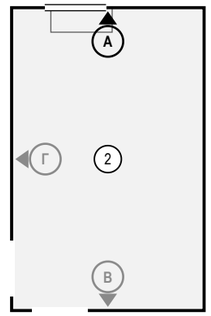

Ведомость отделки (на листе)

Марка	Поверхность	Материал, изделие	Цвет, код	Кол.
О1	стены	окраска, Farrow & Ball Modern Emulsion, матовая, подготовка Q3	Tikkurila G503 «Calla»	7,5 м²
О4	плинтус	плинтус МДФ, h 80 мм, аналог: плинтус МДФ под покраску 80×16	Tikkurila G503 «Calla»	2,1 м
О5	потолок	окраска, Tikkurila Anti-Reflex 2, глубокоматовая, подготовка Q3	Little Greene No. 222 «Loft White»	15,5 м²

Примечания

1. Размеры — в мм от чистовых поверхностей стен; условные обозначения и общие указания — лист 2.

	Лист	№ док.	Подпись	Дата	Проект: Дом 120 м²
Дизайнер	Кырлан А.С.			19.10.26	Развёртка стены А. Холл с лестницей (пом. 2)

Стадия	Лист	Листов
П	60	128

выпуск 19.10.2026 № 66b2a77b4d · стр. 60 из 128

Развёртка стены В


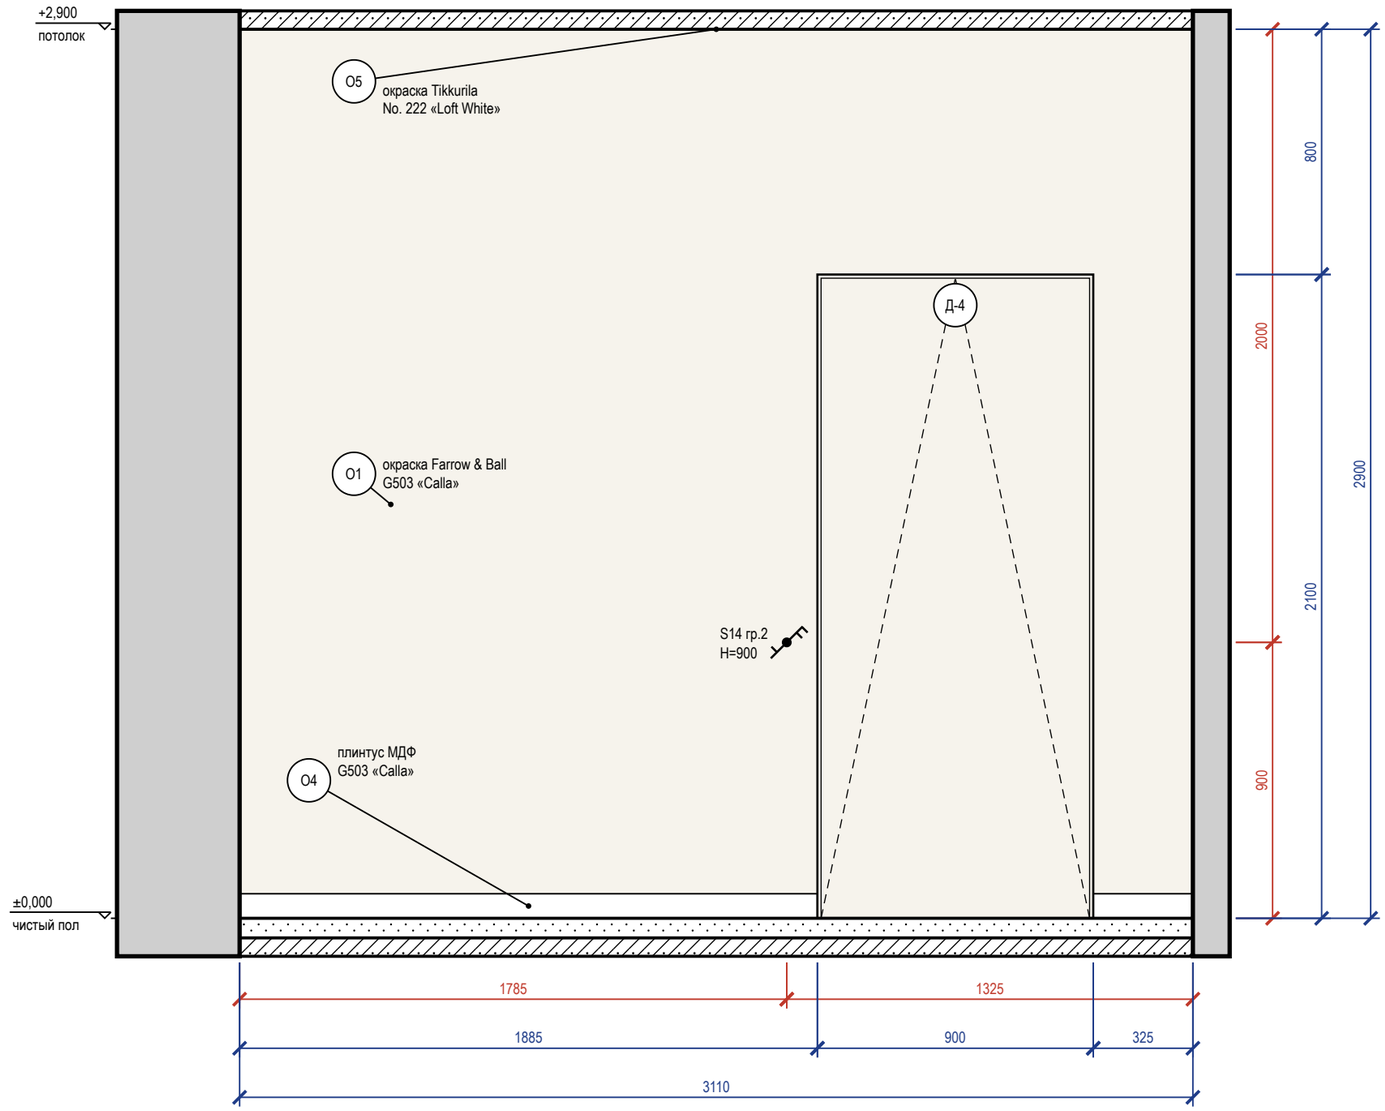


Схема развёрток (М 1:100)

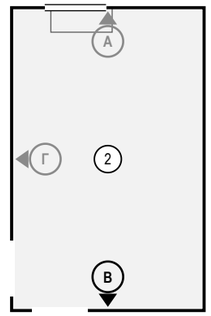

Ведомость отделки (на листе)

Марка	Поверхность	Материал, изделие	Цвет, код	Кол.
О1	стены	окраска, Farrow & Ball Modern Emulsion, матовая, подготовка Q3	Tikkurila G503 «Calla»	7,1 м²
О4	плинтус	плинтус МДФ, h 80 мм, аналог: плинтус МДФ под покраску 80×16	Tikkurila G503 «Calla»	2,2 м
О5	потолок	окраска, Tikkurila Anti-Reflex 2, глубокоматовая, подготовка Q3	Little Greene No. 222 «Loft White»	15,5 м²

Визуализация этой стены



Примечания

1. Размеры — в мм от чистовых поверхностей стен; условные обозначения и общие указания — лист 2.
2. Двери скрытого монтажа — полотно в плоскости стены, отделка стены по полотну, плинтус прерывается у короба (узел — на листе узлов).

					Проект: Дом 120 м²
	Лист	№ док.	Подпись	Дата	Развёртка стены В. Холл с лестницей (пом. 2)
Дизайнер	Кырлан А.С.			19.10.26	

Стадия	Лист	Листов
П	61	128

выпуск 19.10.2026 № 66b2a77b4d · стр. 61 из 128

Развёртка стены Г


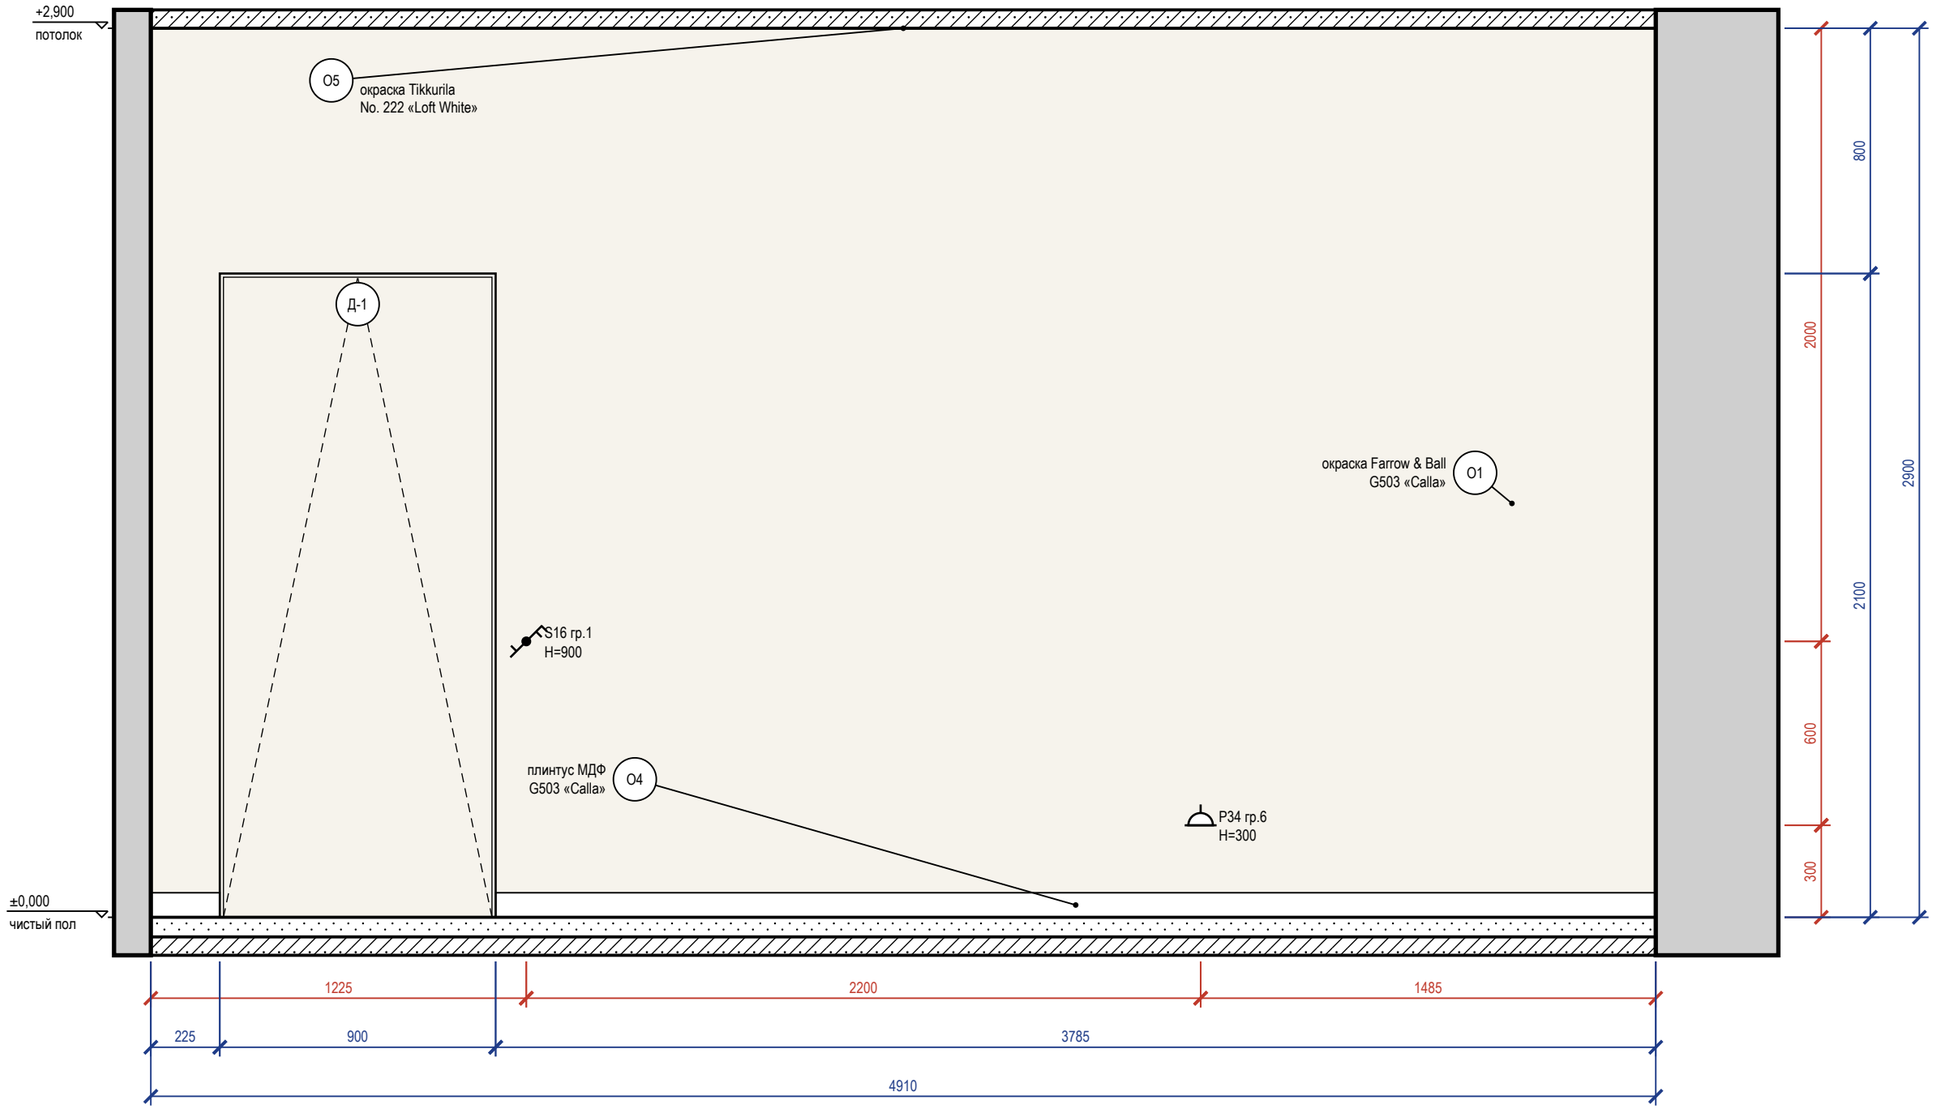


Схема развёрток (М 1:100)

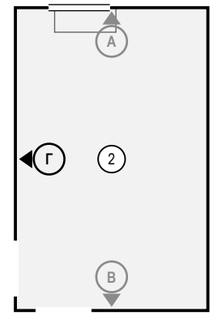

Ведомость отделки (на листе)

Марка	Поверхность	Материал, изделие	Цвет, код	Кол.
О1	стены	окраска, Farrow & Ball Modern Emulsion, матовая, подготовка Q3	Tikkurila G503 «Calla»	12,3 м²
О4	плинтус	плинтус МДФ, h 80 мм, аналог: плинтус МДФ под покраску 80×16	Tikkurila G503 «Calla»	4 м
О5	потолок	окраска, Tikkurila Anti-Reflex 2, глубокоматовая, подготовка Q3	Little Greene No. 222 «Loft White»	15,5 м²

Примечания

1. Размеры — в мм от чистовых поверхностей стен; условные обозначения и общие указания — лист 2.
2. Двери скрытого монтажа — полотно в плоскости стены, отделка стены по полотну, плинтус прерывается у короба (узел — на листе узлов).

					Проект: Дом 120 м²
	Лист	№ док.	Подпись	Дата	Развёртка стены Г. Холл с лестницей (пом. 2)
Дизайнер	Кырлан А.С.			19.10.26	

Стадия	Лист	Листов
П	62	128

выпуск 19.10.2026 № 66b2a77b4d · стр. 62 из 128



					Проект: Дом 120 м²
	Лист	№ док.	Подпись	Дата	
Дизайнер	Кырлан А.С.			19.10.26	Визуализация кабинета

Стадия	Лист	Листов
П	63	128

выпуск 19.10.2026 № 66b2a77b4d · стр. 63 из 128



					Проект: Дом 120 м²	
	Лист	№ док.	Подпись	Дата	Визуализация кабинета	Стадия / Лист / Листов
Дизайнер	Кырлан А.С.			19.10.26		П / 64 / 128

выпуск 19.10.2026 № 66b2a77b4d · стр. 64 из 128

Развёртка стены А


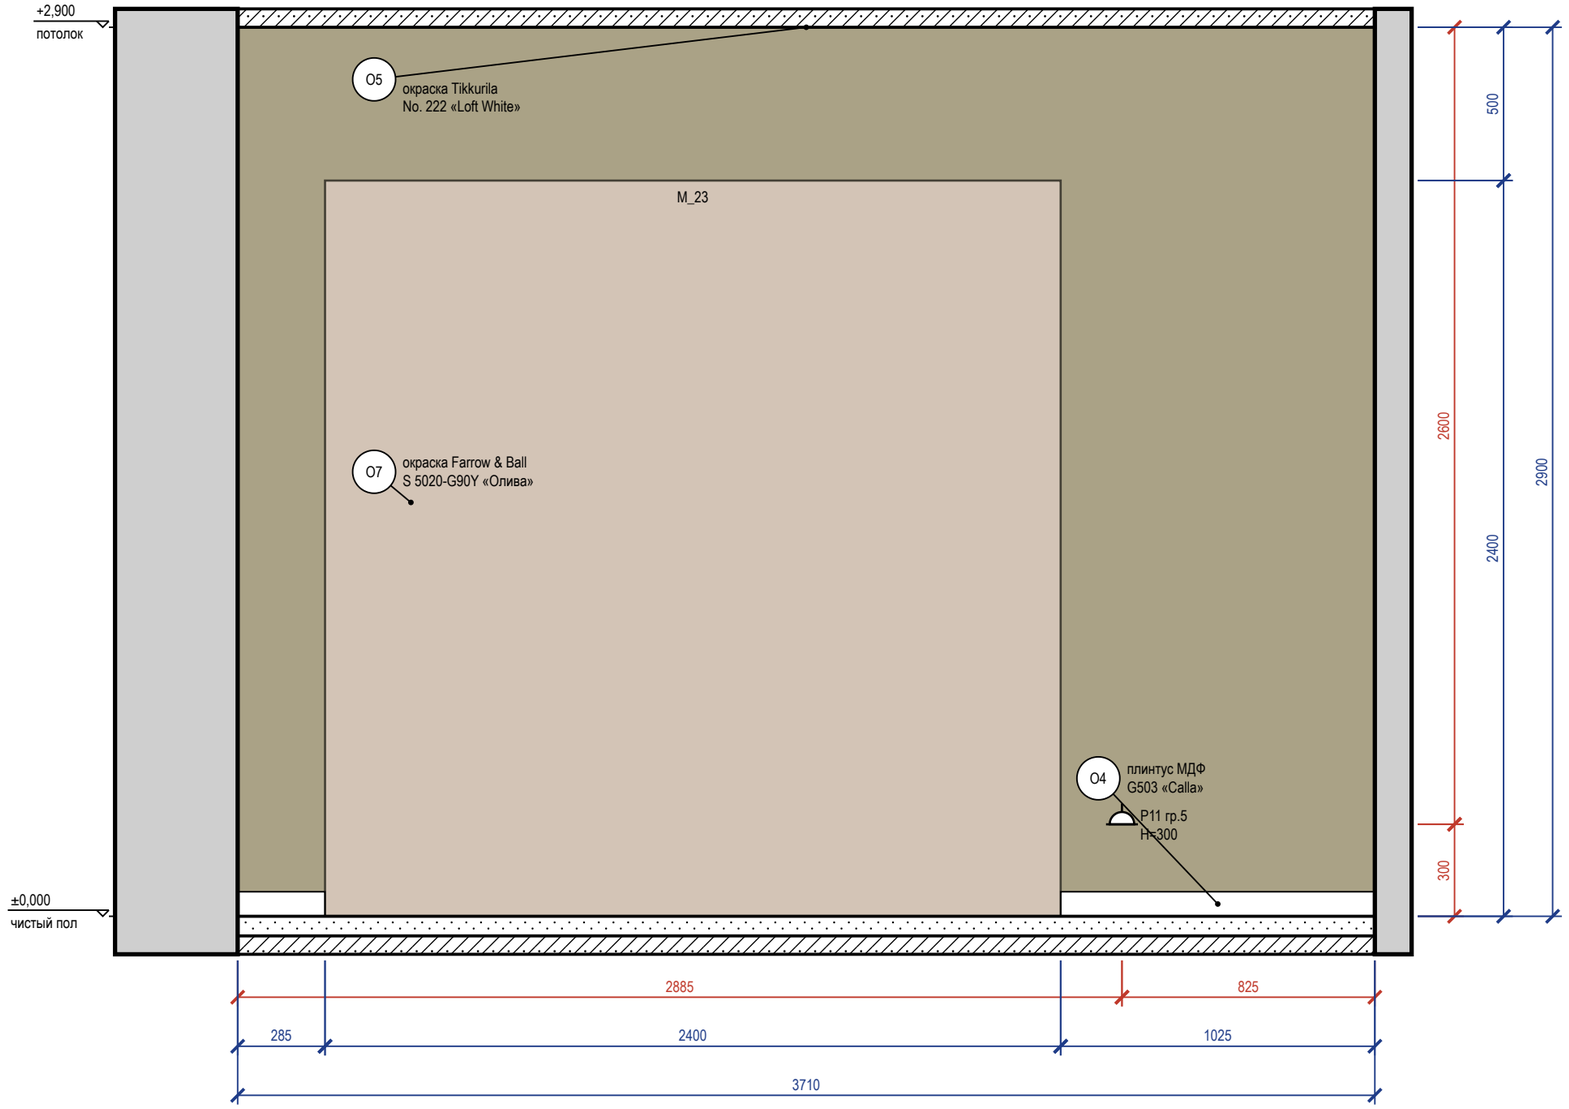


Схема развёрток (М 1:100)

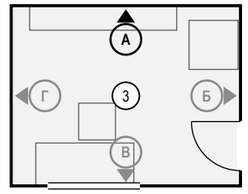

Ведомость отделки (на листе)

Марка	Поверхность	Материал, изделие	Цвет, код	Кол.
О4	плинтус	плинтус МДФ, h 80 мм, аналог: плинтус МДФ под покраску 80×16	Tikkurila G503 «Calla»	1,3 м
О5	потолок	окраска, Tikkurila Anti-Reflex 2, глубокоматовая, подготовка Q3	Little Greene No. 222 «Loft White»	11 м²
О7	акцентная стена	окраска, Farrow & Ball Modern Emulsion, матовая, подготовка Q3	NCS S 5020-G90Y «Олива»	10,8 м²

Визуализация этой стены — лист 63



Примечания

1. Размеры — в мм от чистовых поверхностей стен; условные обозначения и общие указания — лист 2.

					Проект: Дом 120 м²
	Лист	№ док.	Подпись	Дата	Развёртка стены А. Кабинет (пом. 3)
Дизайнер	Кырлан А.С.			19.10.26	

Стадия	Лист	Листов
П	65	128

выпуск 19.10.2026 № 66b2a77b4d · стр. 65 из 128

Развёртка стены Б


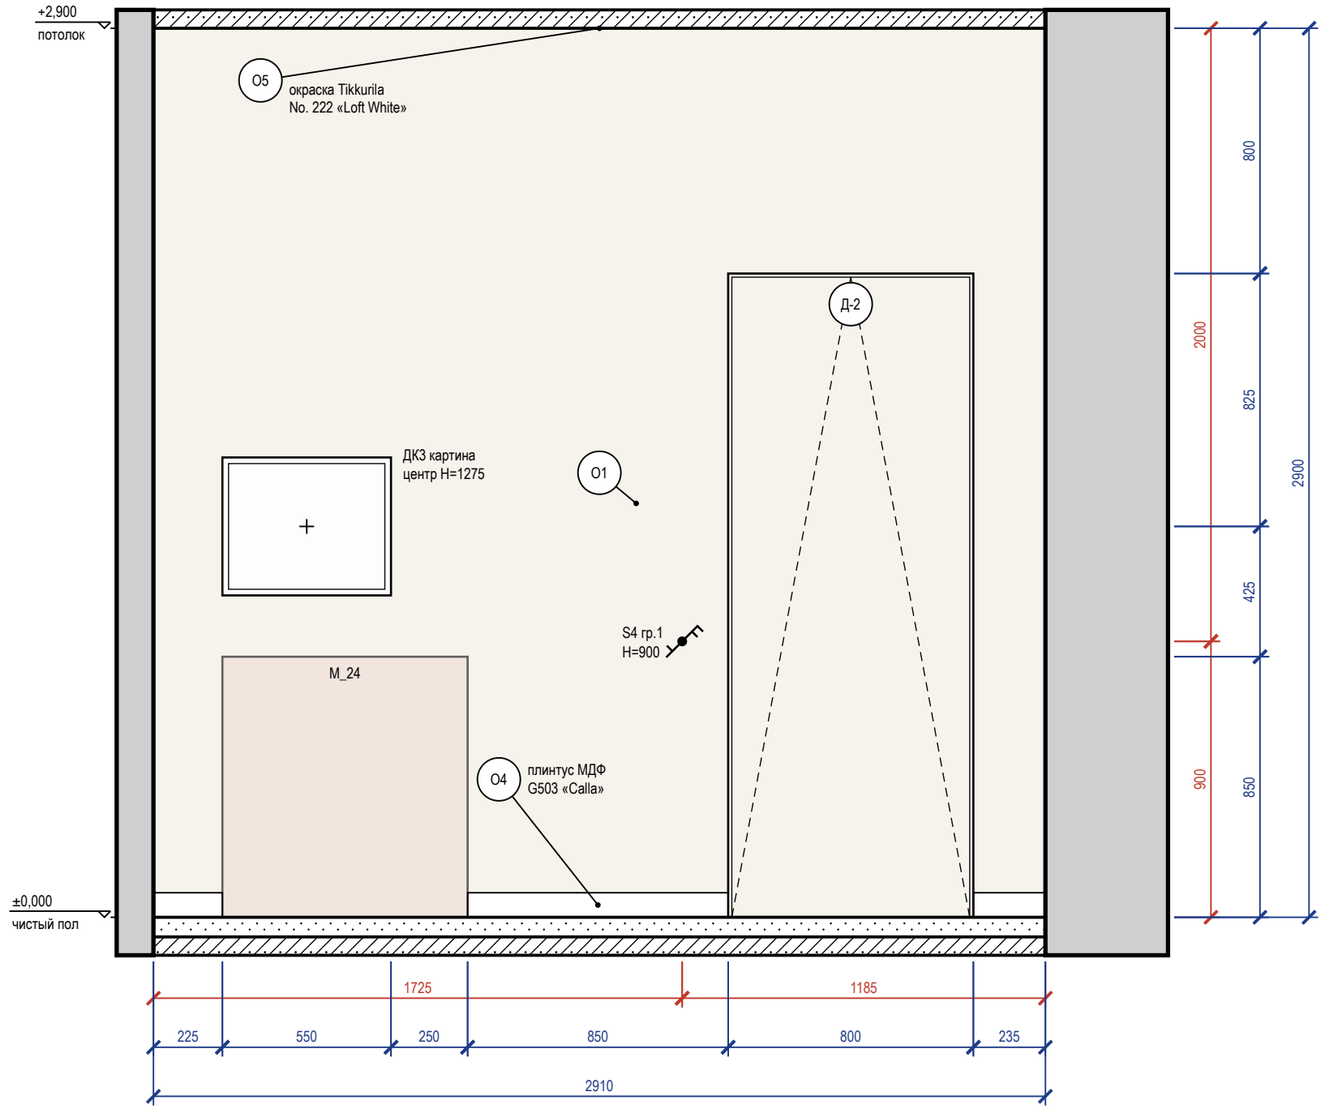


Схема развёрток (М 1:100)

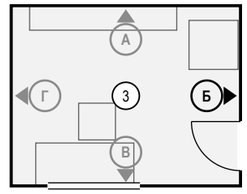

Ведомость отделки (на листе)

Марка	Поверхность	Материал, изделие	Цвет, код	Кол.
О1	стены	окраска, Farrow & Ball Modern Emulsion, матовая, подготовка Q3	Tikkurila G503 «Calla»	6,8 м²
О4	плинтус	плинтус МДФ, h 80 мм, аналог: плинтус МДФ под покраску 80×16	Tikkurila G503 «Calla»	1,3 м
О5	потолок	окраска, Tikkurila Anti-Reflex 2, глубокоматовая, подготовка Q3	Little Greene No. 222 «Loft White»	11 м²

Примечания

1. Размеры — в мм от чистовых поверхностей стен; условные обозначения и общие указания — лист 2.
2. Картины и зеркала крепить к основанию по паспорту изделия (закладные и анкеры — в перечне скрытых работ); крест — ось центра предмета.
3. Двери скрытого монтажа — полотно в плоскости стены, отделка стены по полотну, плинтус прерывается у короба (узел — на листе узлов).

					Проект: Дом 120 м²
	Лист	№ док.	Подпись	Дата	Развёртка стены Б. Кабинет (пом. 3)
Дизайнер	Кырлан А.С.			19.10.26	

Стадия	Лист	Листов
П	66	128

выпуск 19.10.2026 № 66b2a77b4d · стр. 66 из 128

Развёртка стены В


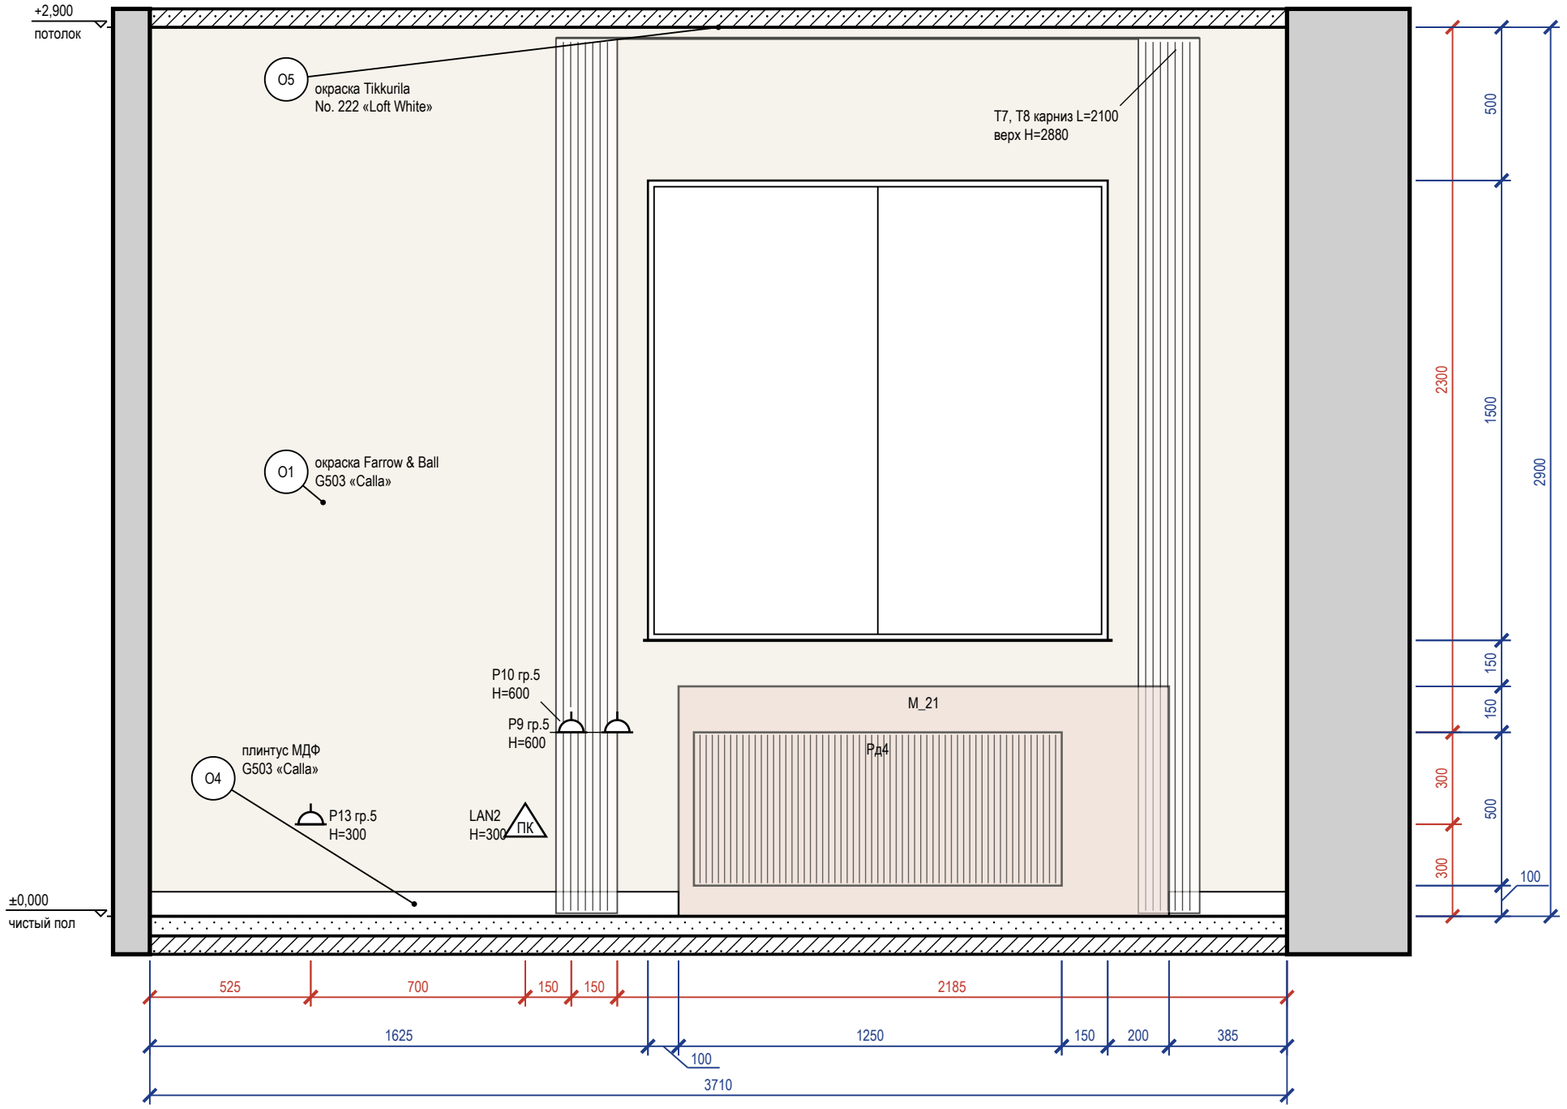



Схема развёрток (М 1:100)

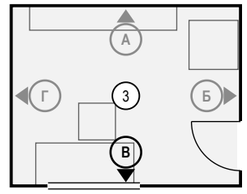

Ведомость отделки (на листе)

Марка	Поверхность	Материал, изделие	Цвет, код	Кол.
О1	стены	окраска, Farrow & Ball Modern Emulsion, матовая, подготовка Q3	Tikkurila G503 «Calla»	8,5 м²
О4	плинтус	плинтус МДФ, h 80 мм, аналог: плинтус МДФ под покраску 80×16	Tikkurila G503 «Calla»	2,1 м
О5	потолок	окраска, Tikkurila Anti-Reflex 2, глубокоматовая, подготовка Q3	Little Greene No. 222 «Loft White»	11 м²

Визуализация этой стены — лист 64

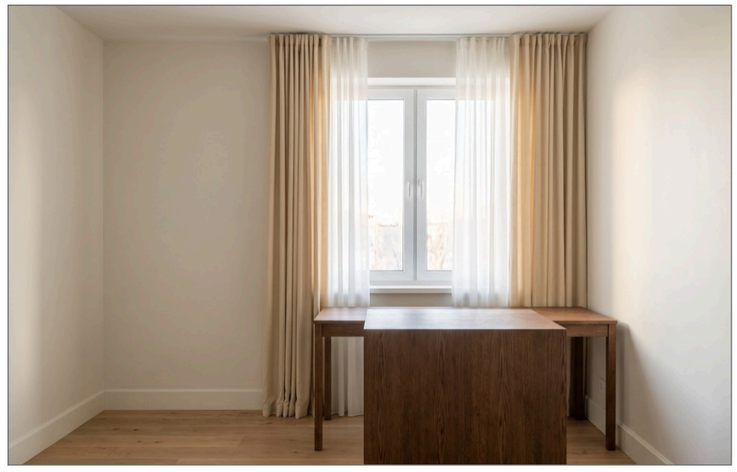

Примечания

1. Размеры — в мм от чистовых поверхностей стен; условные обозначения и общие указания — лист 2.
2. Карнизы (шины) — по ведомости текстиля декоратора; длина L и верх H — по развёртке, крепление — до окраски потолка.
3. Линии узора (швы плитки, складки штор, рёбра радиаторов) прерываются у знаков и выносок — просвет между линиями не менее 0,7 мм.

					Проект: Дом 120 м²
	Лист	№ док.	Подпись	Дата	Развёртка стены В. Кабинет (пом. 3)
Дизайнер	Кырлан А.С.			19.10.26	

Стадия	Лист	Листов
П	67	128

выпуск 19.10.2026 № 66b2a77b4d · стр. 67 из 128

Развёртка стены Г


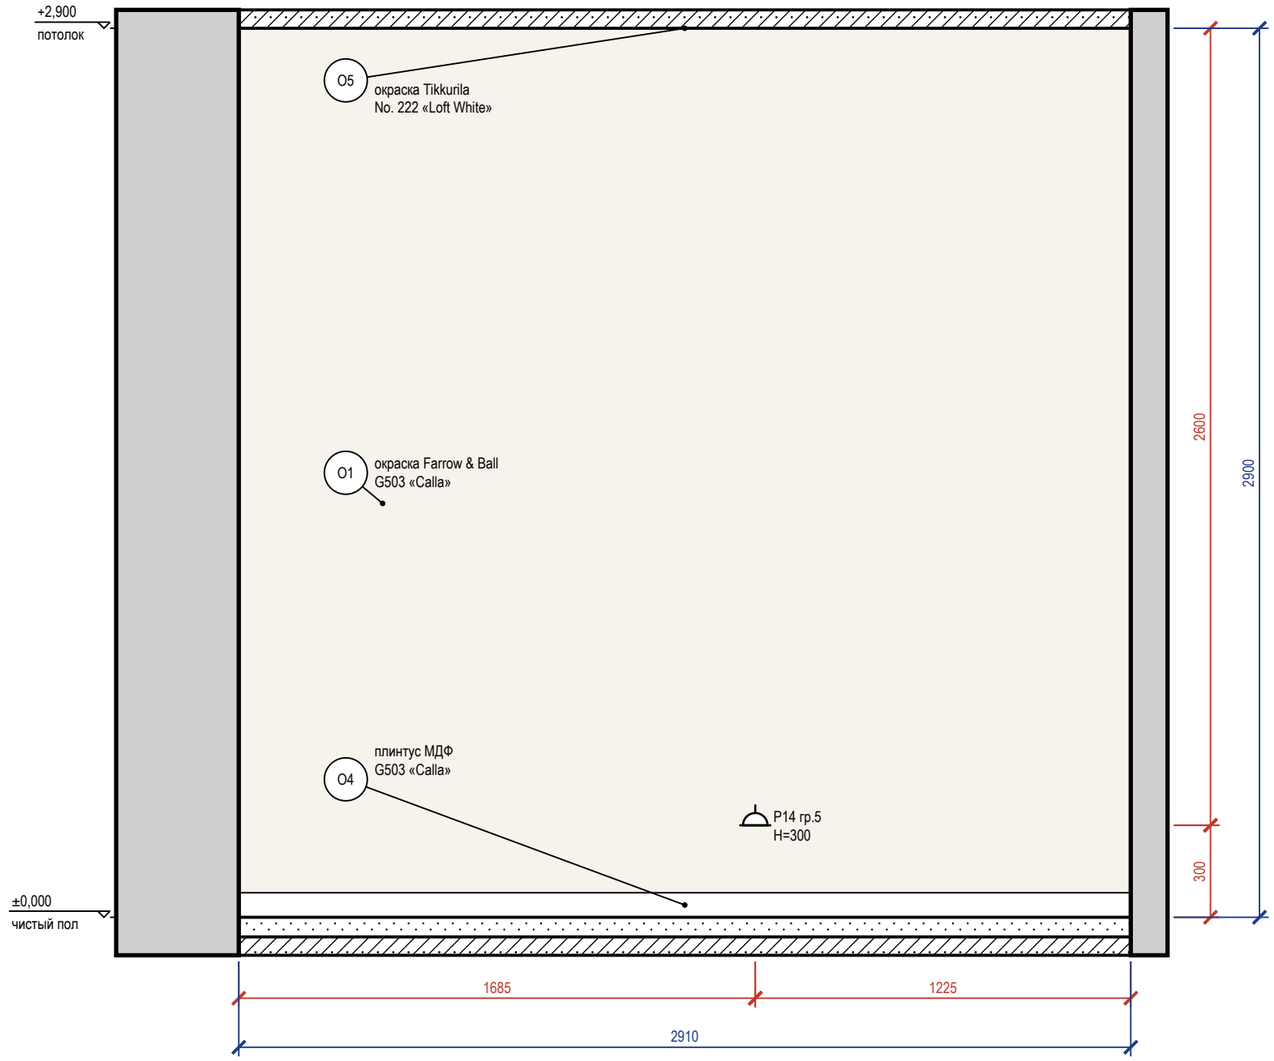


Схема развёрток (М 1:100)

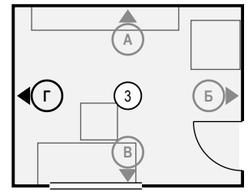

Ведомость отделки (на листе)

Марка	Поверхность	Материал, изделие	Цвет, код	Кол.
О1	стены	окраска, Farrow & Ball Modern Emulsion, матовая, подготовка Q3	Tikkurila G503 «Calla»	8,4 м²
О4	плинтус	плинтус МДФ, h 80 мм, аналог: плинтус МДФ под покраску 80×16	Tikkurila G503 «Calla»	2,9 м
О5	потолок	окраска, Tikkurila Anti-Reflex 2, глубокоматовая, подготовка Q3	Little Greene No. 222 «Loft White»	11 м²

Примечания

1. Размеры — в мм от чистовых поверхностей стен; условные обозначения и общие указания — лист 2.

					Проект: Дом 120 м²
	Лист	№ док.	Подпись	Дата	Развёртка стены Г. Кабинет (пом. 3)
Дизайнер	Кырлан А.С.			19.10.26	

Стадия	Лист	Листов
П	68	128

выпуск 19.10.2026 № 66b2a77b4d · стр. 68 из 128



					Проект: Дом 120 м²
	Лист	№ док.	Подпись	Дата	
Дизайнер	Кырлан А.С.			19.10.26	Визуализация: Санузел гостевой

Стадия	Лист	Листов
П	69	128

выпуск 19.10.2026 № 66b2a77b4d · стр. 69 из 128

Развёртка стены А


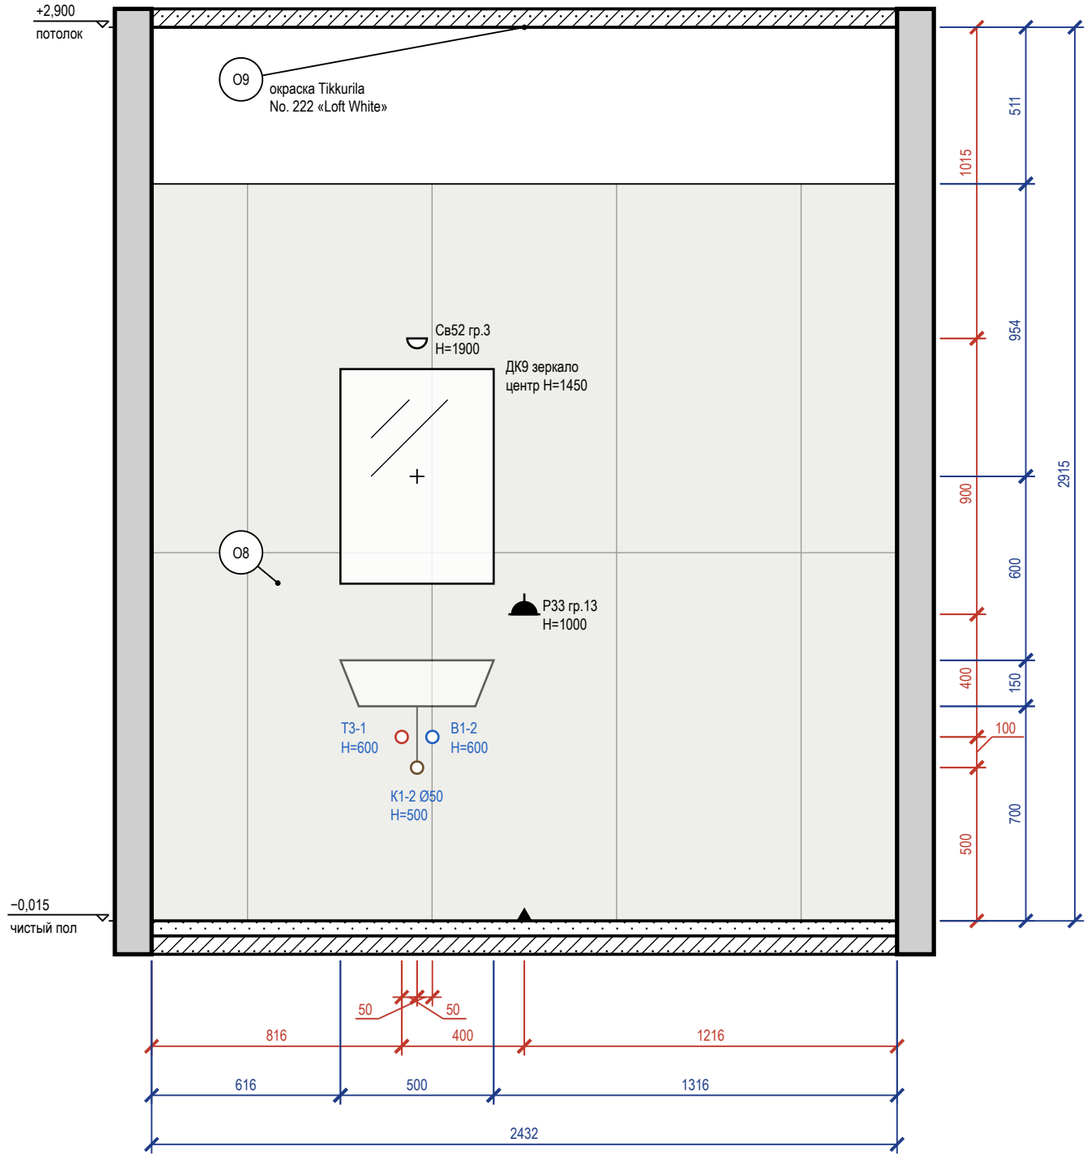


Схема развёрток (М 1:100)

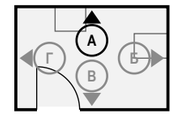

Ведомость отделки (на листе)

Марка	Поверхность	Материал, изделие	Цвет, код	Кол.
О8	стены	облицовка плиткой, Atlas Concorde Marvel Travertine, 600×1200×9 мм, А8UZ, затирка CG2WA	Atlas Concorde A8UZ «Marvel Travertine»	5,8 м²
О9	потолок	окраска, Tikkurila Luja 7, матовая, подготовка Q3	Little Greene No. 222 «Loft White»	4,2 м²

Примечания

1. Размеры — в мм от чистовых поверхностей стен; условные обозначения и общие указания — лист 2.
2. Схема мебели, приборов и декора не является технической документацией для производства мебели; габариты — по паспортам изделий.
3. Выводы ВК — коды и высоты по листу выводов сантехники.
4. Облицовка — по сетке швов 2 мм, раскладка от оси стены (треугольник у пола), целые ряды от пола; подрезки — по листу раскладки плитки.
5. Гидроизоляция в 2 слоя, заход на стены 200 мм — до облицовки, с актом скрытых работ и тестом проливом (узел — на листе узлов).
6. Картины и зеркала крепить к основанию по паспорту изделия (закладные и анкеры — в перечне скрытых работ); крест — ось центра предмета.

					Проект: Дом 120 м²
	Лист	№ док.	Подпись	Дата	Развёртка стены А. Санузел гостевой (пом. 4)
Дизайнер	Кырлан А.С.			19.10.26	

Стадия	Лист	Листов
П	70	128

выпуск 19.10.2026 № 66b2a77b4d · стр. 70 из 128

Развёртка стены Б


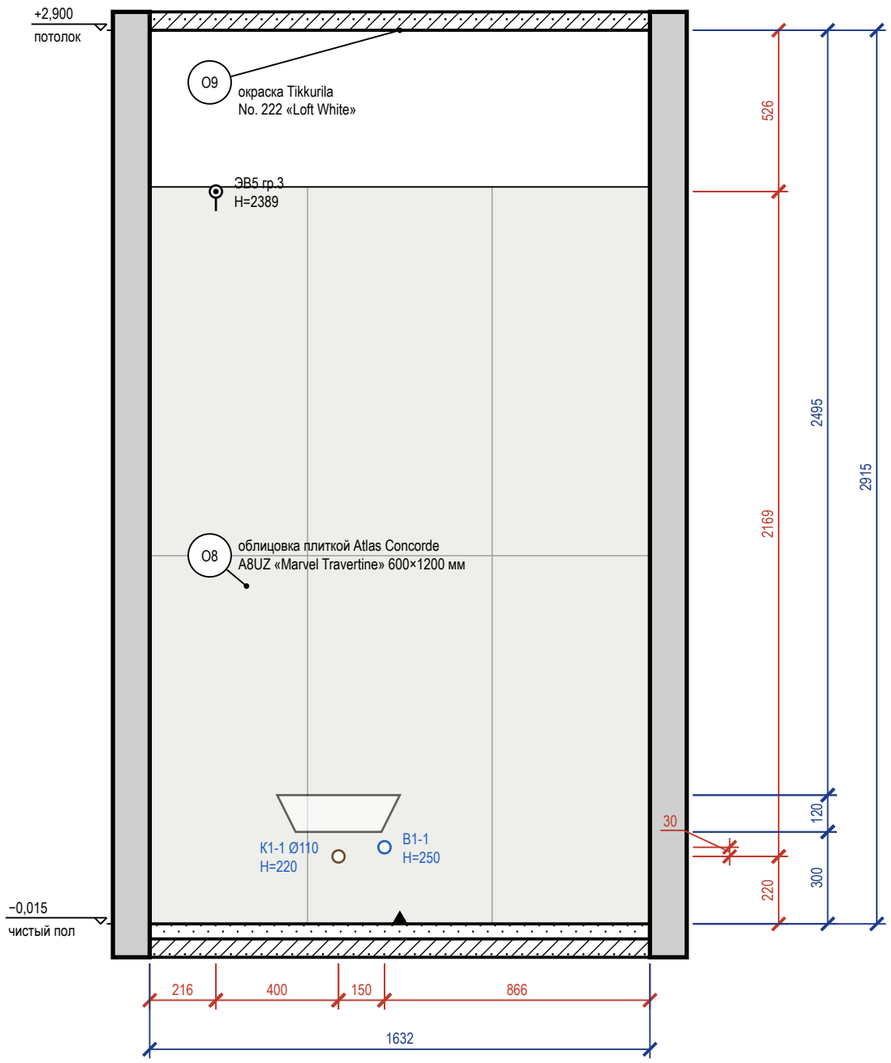


Схема развёрток (М 1:100)

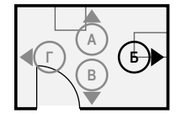

Ведомость отделки (на листе)


Марка	Поверхность	Материал, изделие	Цвет, код	Кол.
O8	стены	облицовка плиткой, Atlas Concorde Marvel Travertine, 600×1200×9 мм, A8UZ, затирка CG2WA	Atlas Concorde A8UZ «Marvel Travertine»	3,9 м²
O9	потолок	окраска, Tikkurila Luja 7, матовая, подготовка Q3	Little Greene No. 222 «Loft White»	4,2 м²

Визуализация этой стены — лист 69



3 Короб стояков К1-1 с люком и звукоизоляцией (М 1:20)

Узел 3 — лист С3

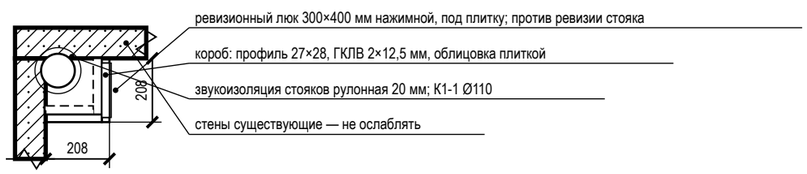

Примечания


1. Размеры — в мм от чистовых поверхностей стен; условные обозначения и общие указания — лист 2.
2. Схема мебели, приборов и декора не является технической документацией для производства мебели; габариты — по паспортам изделий.
3. Выводы ВК — коды и высоты по листу выводов сантехники.
4. Облицовка — по сетке швов 2 мм, раскладка от оси стены (треугольник у пола), целые ряды от пола; подрезки — по листу раскладки плитки.
5. Гидроизоляция в 2 слоя, заход на стены 200 мм — до облицовки, с актом скрытых работ и тестом проливом (узел — на листе узлов).

					Проект: Дом 120 м²
	Лист	№ док.	Подпись	Дата	Развёртка стены Б. Санузел гостевой (пом. 4)
Дизайнер	Кырлан А.С.			19.10.26	

Стадия	Лист	Листов
П	71	128

выпуск 19.10.2026 № 66b2a77b4d · стр. 71 из 128

Развёртка стены В

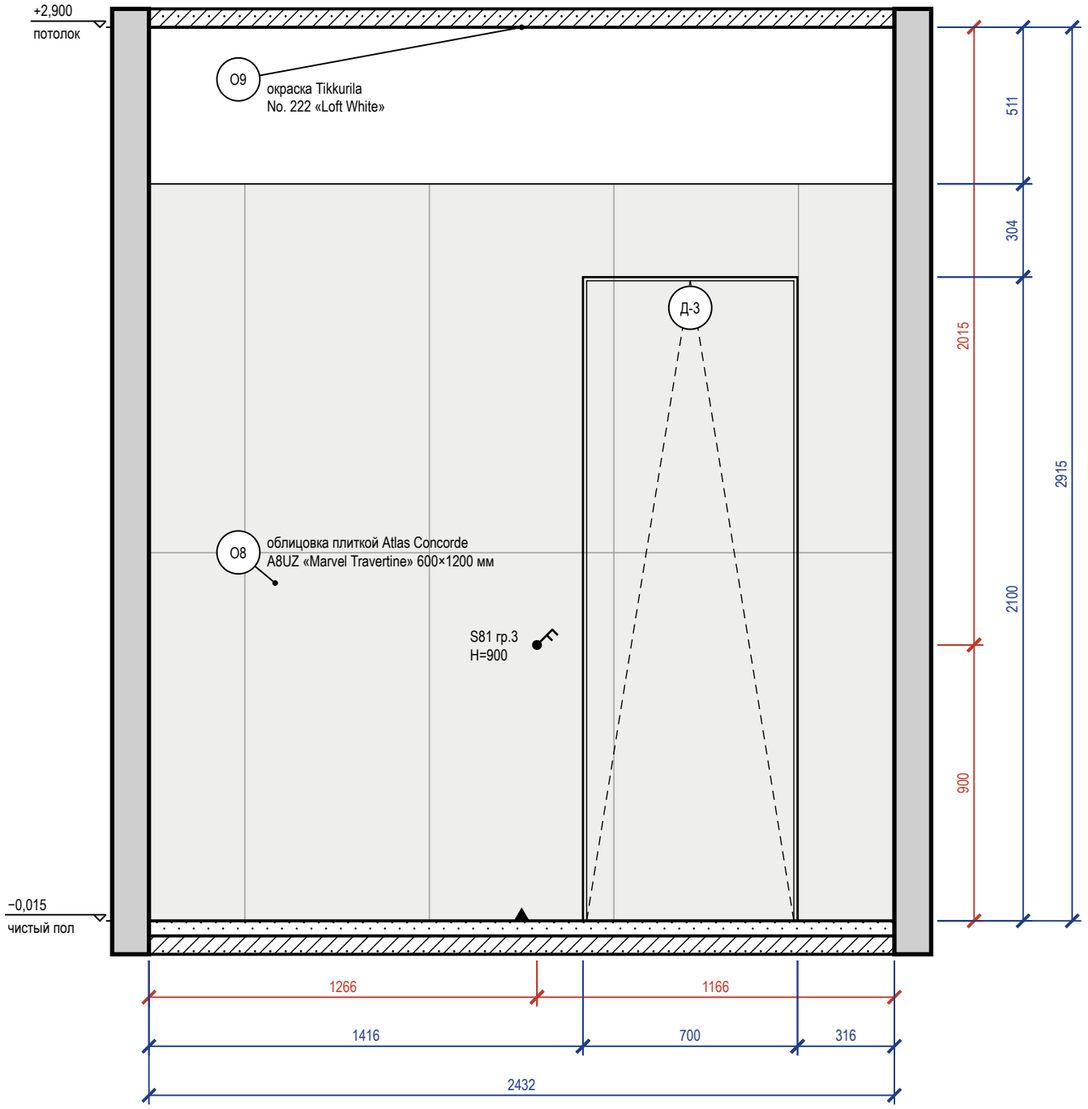

Развёртка стены Г


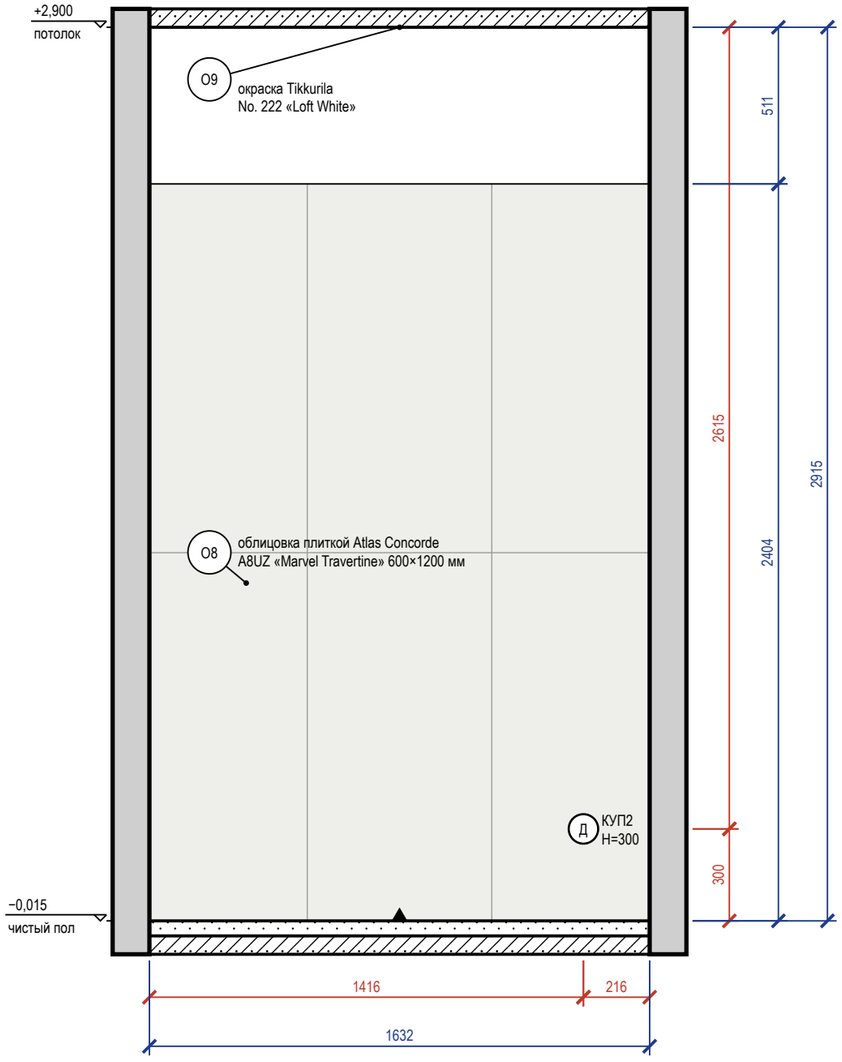


Схема развёрток (М 1:100)

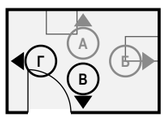

Ведомость отделки (на листе)

Марка	Поверхность	Материал, изделие	Цвет, код	Кол.
О8	стены	облицовка плиткой, Atlas Concorde Marvel Travertine, 600×1200×9 мм, A8UZ, затирка CG2WA	Atlas Concorde A8UZ «Marvel Travertine»	8,3 м²
О9	потолок	окраска, Tikkurila Luja 7, матовая, подготовка Q3	Little Greene No. 222 «Loft White»	4,2 м²

Примечания

1. Размеры — в мм от чистовых поверхностей стен; условные обозначения и общие указания — лист 2.
2. Облицовка — по сетке швов 2 мм, раскладка от оси стены (треугольник у пола), целые ряды от пола; подрезки — по листу раскладки плитки.
3. Гидроизоляция в 2 слоя, заход на стены 200 мм — до облицовки, с актом скрытых работ и тестом проливом (узел — на листе узлов).
4. Двери скрытого монтажа — полотно в плоскости стены, отделка стены по полотну, плинтус прерывается у короба (узел — на листе узлов).

					Проект: Дом 120 м²
	Лист	№ док.	Подпись	Дата	Развёртки стен В, Г. Санузел гостевой (пом. 4)
Дизайнер	Кырлан А.С.			19.10.26	

Стадия	Лист	Листов
П	72	128

выпуск 19.10.2026 № 66b2a77b4d · стр. 72 из 128



					Проект: Дом 120 м²
	Лист	№ док.	Подпись	Дата	
Дизайнер	Кырлан А.С.			19.10.26	Визуализация прихожей
					Стадия: П; Лист: 73; Листов: 128

выпуск 19.10.2026 № 66b2a77b4d · стр. 73 из 128



					Проект: Дом 120 м²
	Лист	№ док.	Подпись	Дата	Визуализация прихожей
Дизайнер	Кырлан А.С.			19.10.26	

Стадия	Лист	Листов
П	74	128

выпуск 19.10.2026 № 66b2a77b4d · стр. 74 из 128

Развёртка стены А1


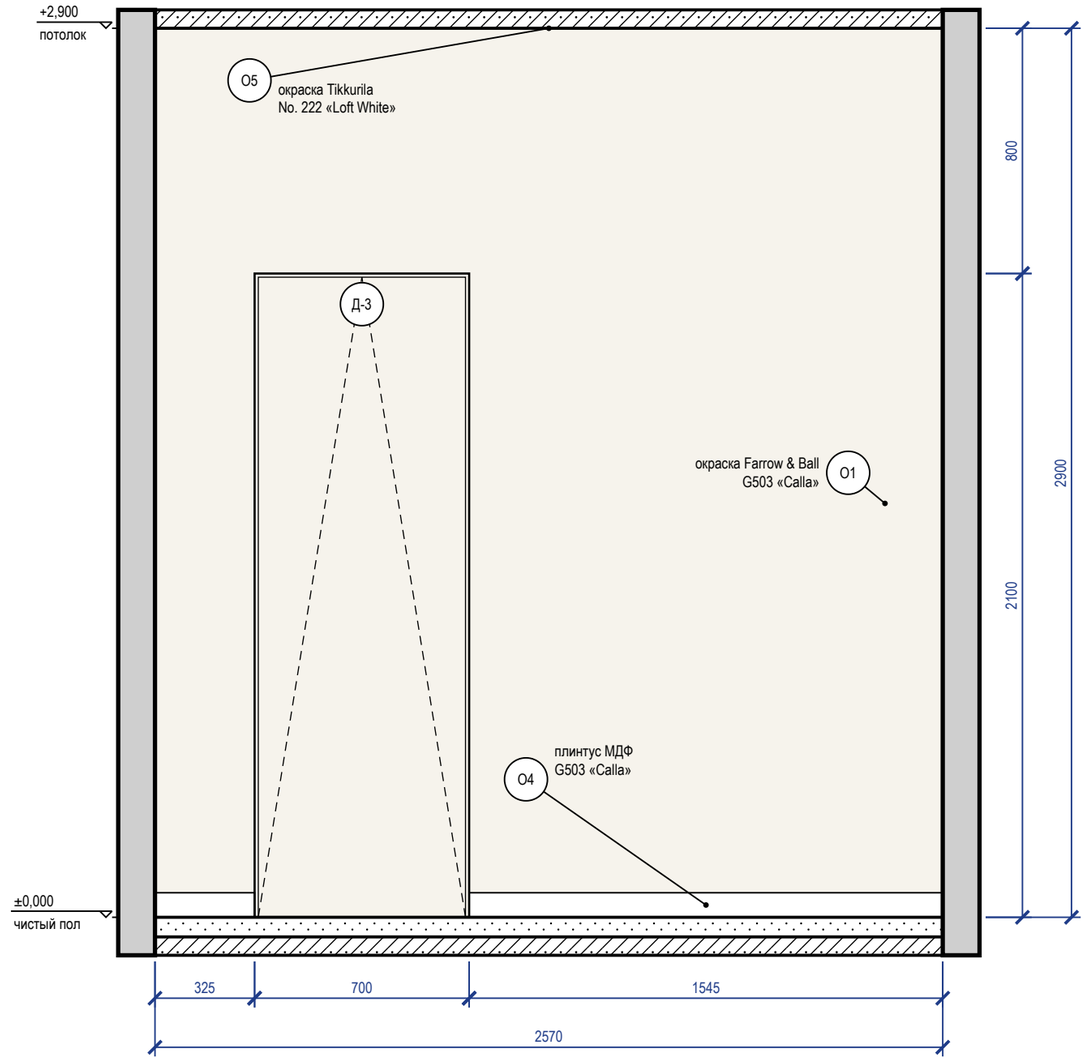


Схема развёрток (М 1:100)

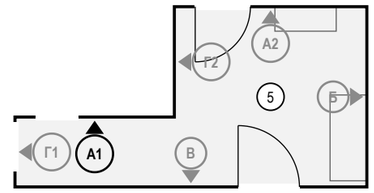

Ведомость отделки (на листе)

Марка	Поверхность	Материал, изделие	Цвет, код	Кол.
О1	стены	окраска, Farrow & Ball Modern Emulsion, матовая, подготовка Q3	Tikkurila G503 «Calla»	6 м²
О4	плинтус	плинтус МДФ, h 80 мм, аналог: плинтус МДФ под покраску 80×16	Tikkurila G503 «Calla»	1,9 м
О5	потолок	окраска, Tikkurila Anti-Reflex 2, глубокоматовая, подготовка Q3	Little Greene No. 222 «Loft White»	12,2 м²

Примечания

1. Размеры — в мм от чистовых поверхностей стен; условные обозначения и общие указания — лист 2.
2. Двери скрытого монтажа — полотно в плоскости стены, отделка стены по полотну, плинтус прерывается у короба (узел — на листе узлов).

					Проект: Дом 120 м²
	Лист	№ док.	Подпись	Дата	Развёртка стены А1. Прихожая (пом. 5)
Дизайнер	Кырлан А.С.			19.10.26	

Стадия	Лист	Листов
П	75	128

выпуск 19.10.2026 № 66b2a77b4d · стр. 75 из 128

Развёртка стены А2


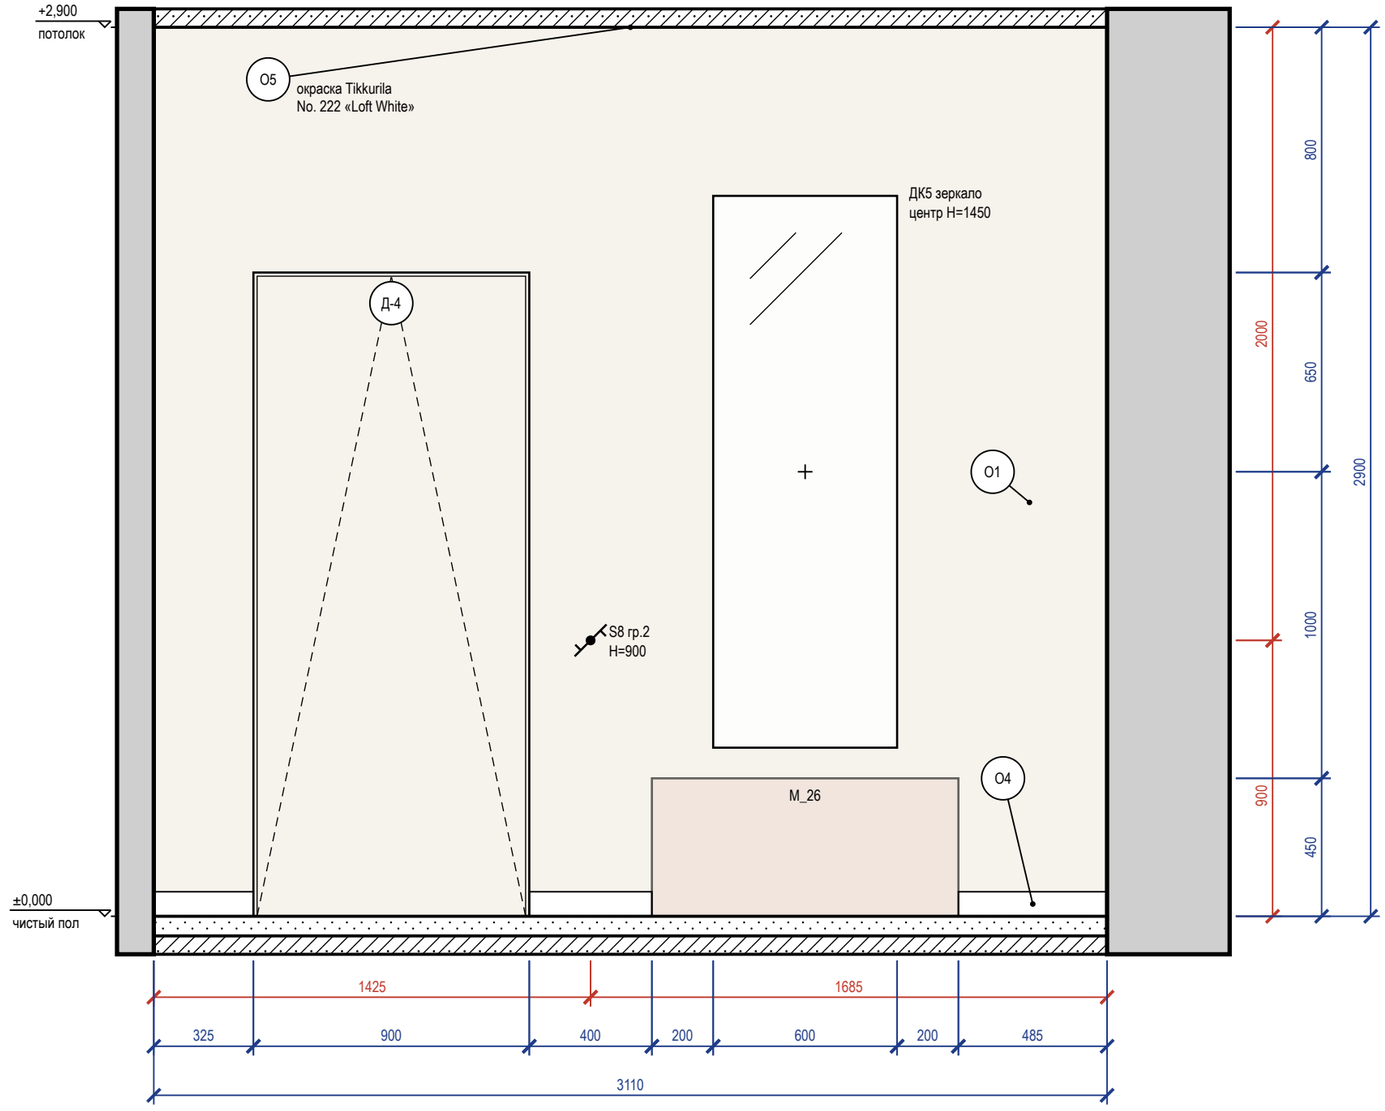


Схема развёрток (М 1:100)

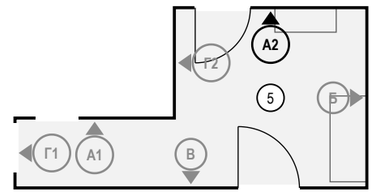

Ведомость отделки (на листе)

Марка	Поверхность	Материал, изделие	Цвет, код	Кол.
О1	стены	окраска, Farrow & Ball Modern Emulsion, матовая, подготовка Q3	Tikkurila G503 «Calla»	7,1 м²
О4	плинтус	плинтус МДФ, h 80 мм, аналог: плинтус МДФ под покраску 80×16	Tikkurila G503 «Calla»	1,2 м
О5	потолок	окраска, Tikkurila Anti-Reflex 2, глубокоматовая, подготовка Q3	Little Greene No. 222 «Loft White»	12,2 м²

Визуализация этой стены — лист 73



Примечания

1. Размеры — в мм от чистовых поверхностей стен; условные обозначения и общие указания — лист 2.
2. Картины и зеркала крепить к основанию по паспорту изделия (закладные и анкеры — в перечне скрытых работ); крест — ось центра предмета.
3. Двери скрытого монтажа — полотно в плоскости стены, отделка стены по полотну, плинтус прерывается у короба (узел — на листе узлов).

	Лист	№ док.	Подпись	Дата
Дизайнер	Кырлан А.С.			19.10.26

Проект: Дом 120 м²

Развёртка стены А2. Прихожая (пом. 5)

Стадия	Лист	Листов
П	76	128

выпуск 19.10.2026 № 66b2a77b4d · стр. 76 из 128

Развёртка стены Б


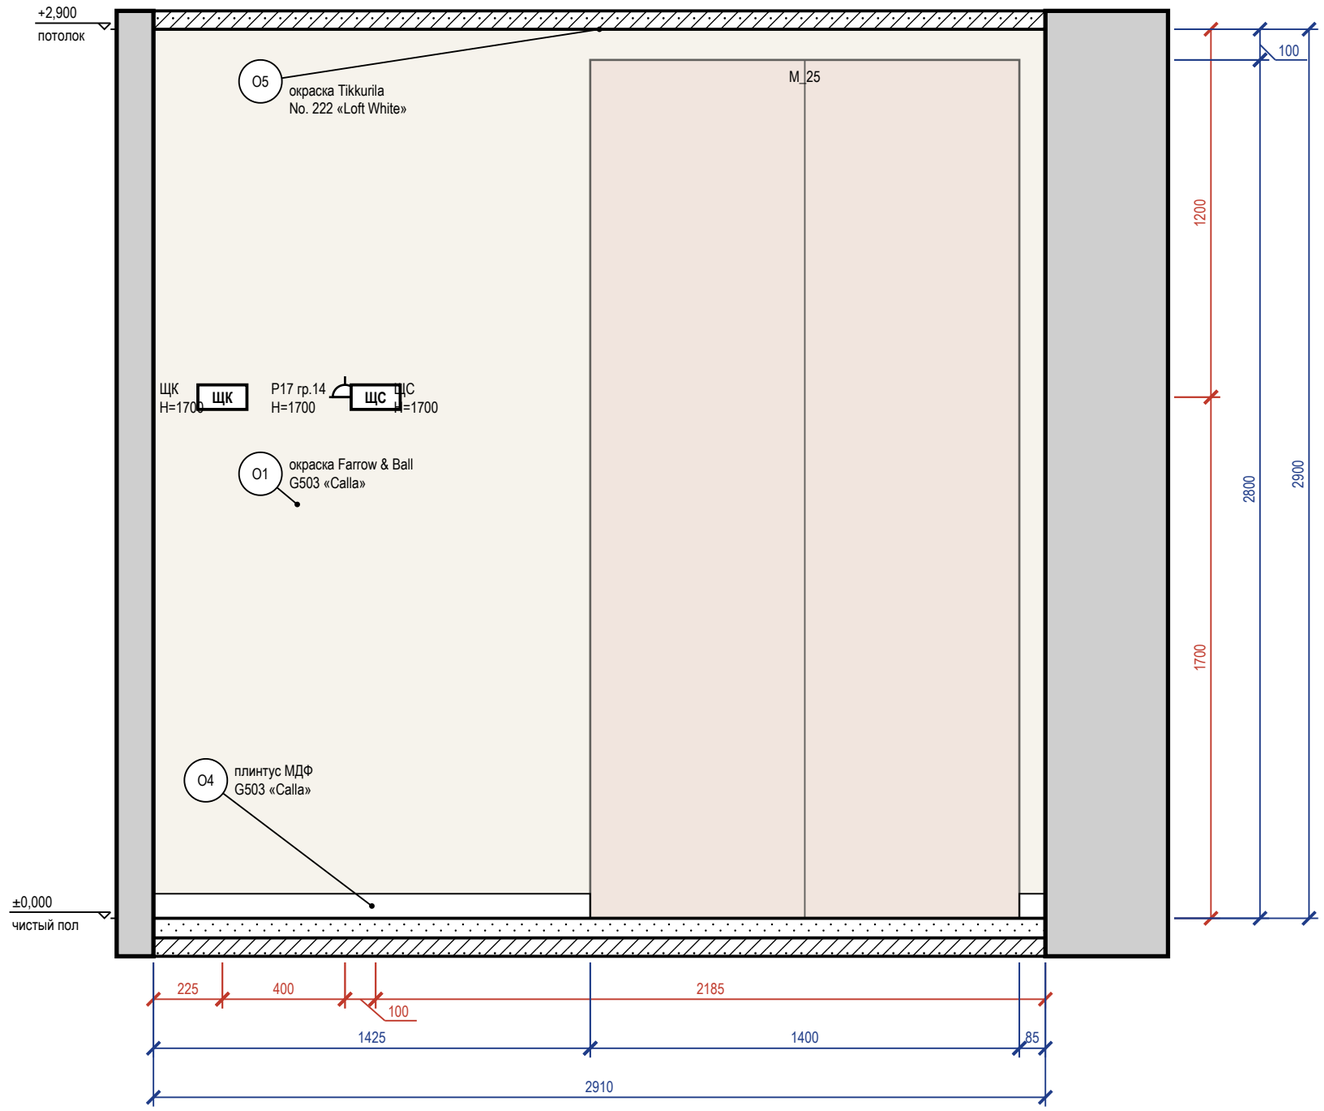



Схема развёрток (М 1:100)

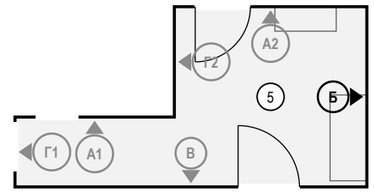

Ведомость отделки (на листе)

Марка	Поверхность	Материал, изделие	Цвет, код	Кол.
О1	стены	окраска, Farrow & Ball Modern Emulsion, матовая, подготовка Q3	Tikkurila G503 «Calla»	8,4 м²
О4	плинтус	плинтус МДФ, h 80 мм, аналог: плинтус МДФ под покраску 80×16	Tikkurila G503 «Calla»	1,5 м
О5	потолок	окраска, Tikkurila Anti-Reflex 2, глубокоматовая, подготовка Q3	Little Greene No. 222 «Loft White»	12,2 м²

Визуализация этой стены — лист 74

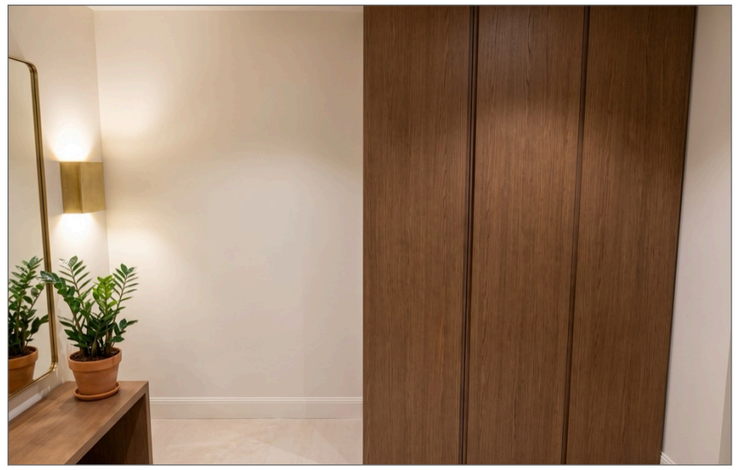

Примечания

1. Размеры — в мм от чистовых поверхностей стен; условные обозначения и общие указания — лист 2.

					Проект: Дом 120 м²
	Лист	№ док.	Подпись	Дата	Развёртка стены Б. Прихожая (пом. 5)
Дизайнер	Кырлан А.С.			19.10.26	

Стадия	Лист	Листов
П	77	128

выпуск 19.10.2026 № 66b2a77b4d · стр. 77 из 128

Развёртка стены В


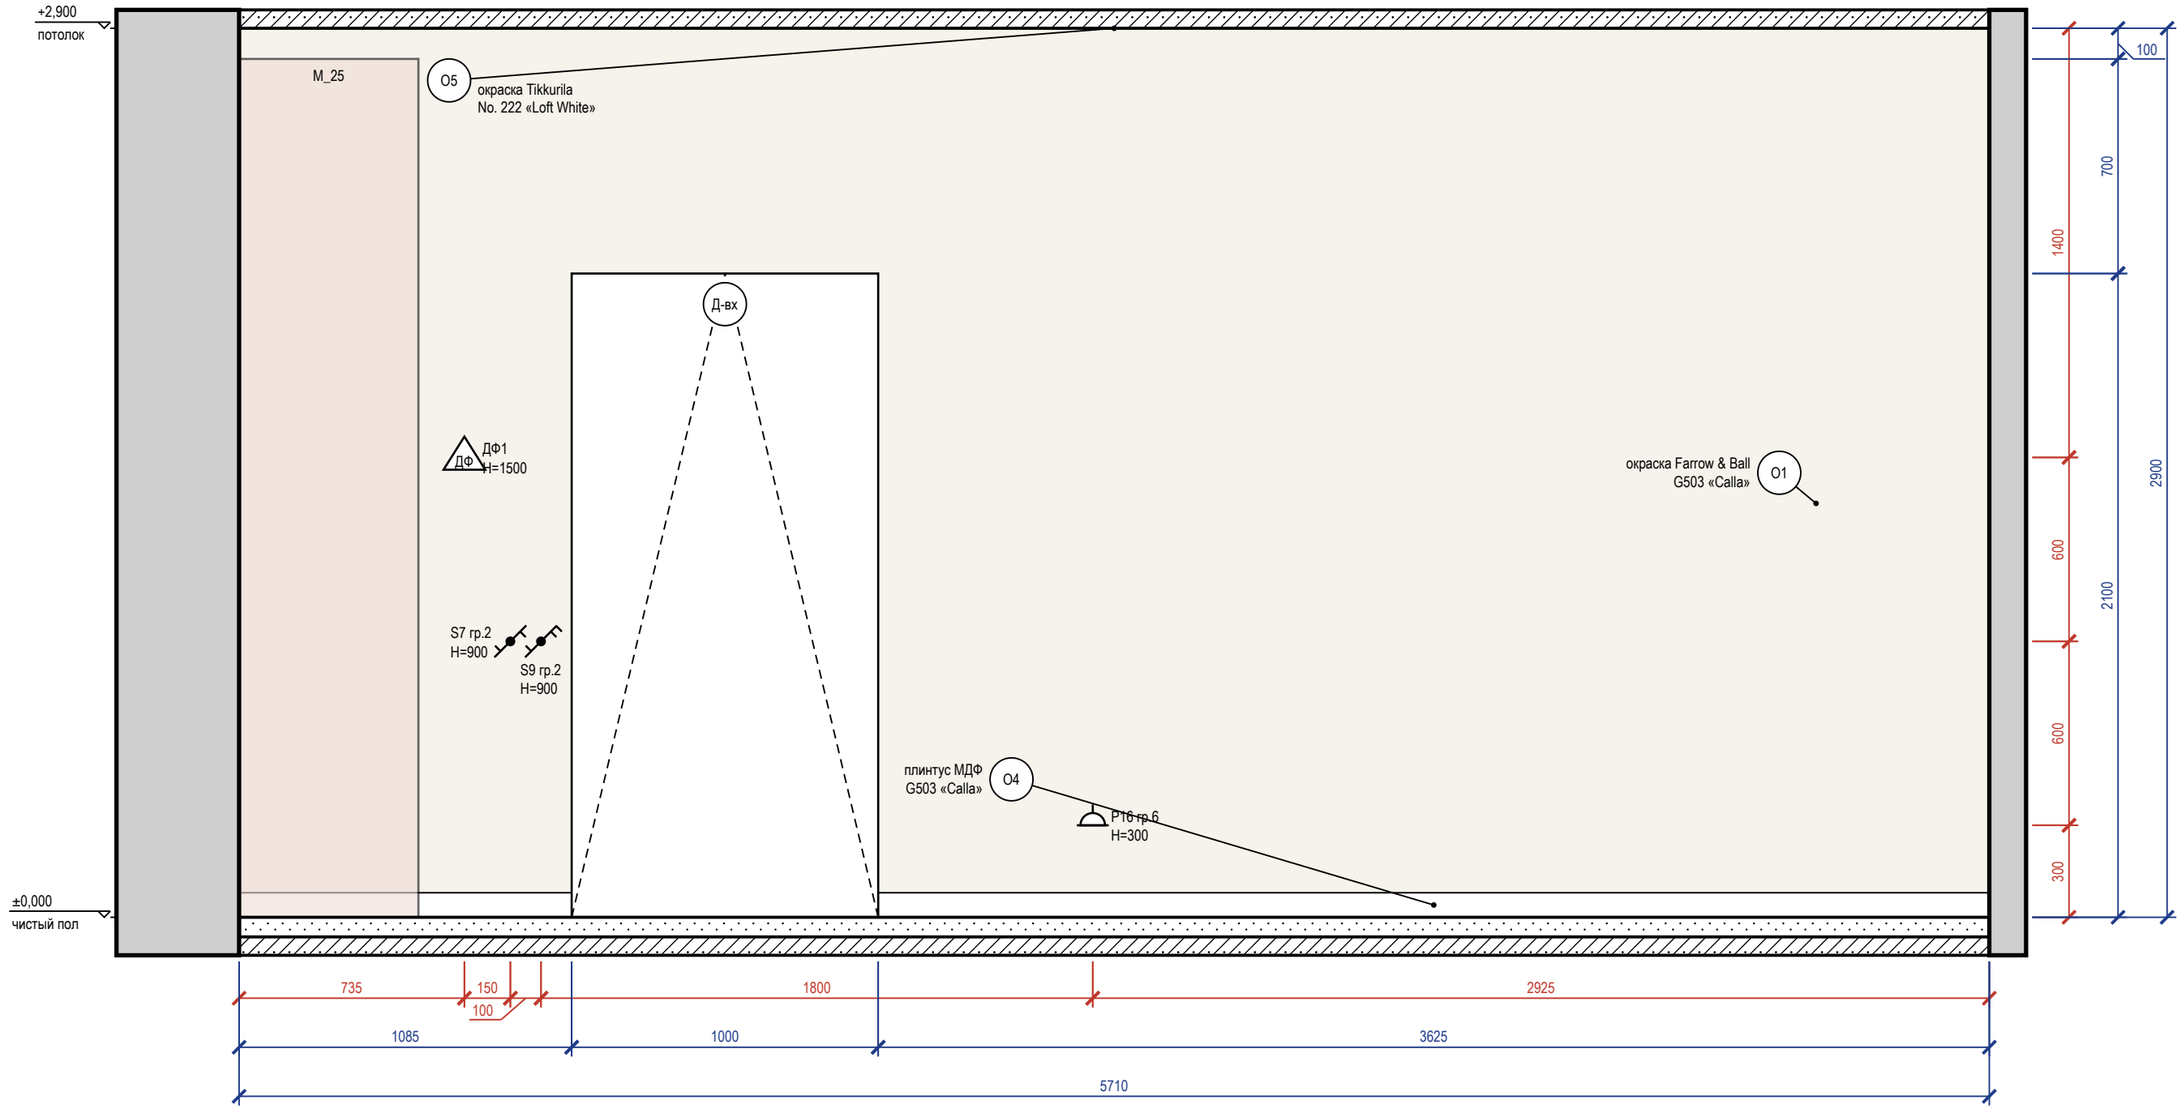


Схема развёрток (М 1:100)

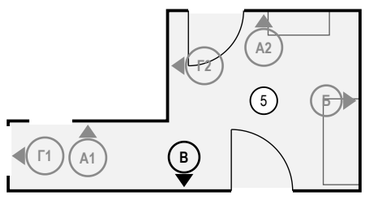

Ведомость отделки (на листе)

Марка	Поверхность	Материал, изделие	Цвет, код	Кол.
О1	стены	окраска, Farrow & Ball Modern Emulsion, матовая, подготовка Q3	Tikkurila G503 «Calla»	14,5 м²
О4	плинтус	плинтус МДФ, h 80 мм, аналог: плинтус МДФ под покраску 80×16	Tikkurila G503 «Calla»	4,7 м
О5	потолок	окраска, Tikkurila Anti-Reflex 2, глубокоматовая, подготовка Q3	Little Greene No. 222 «Loft White»	12,2 м²

Примечания


1. Размеры — в мм от чистовых поверхностей стен; условные обозначения и общие указания — лист 2.

					Проект: Дом 120 м²
	Лист	№ док.	Подпись	Дата	Развёртка стены В. Прихожая (пом. 5)
Дизайнер	Кырлан А.С.			19.10.26	

Стадия	Лист	Листов
П	78	128

выпуск 19.10.2026 № 66b2a77b4d · стр. 78 из 128

Развёртка стены Г1

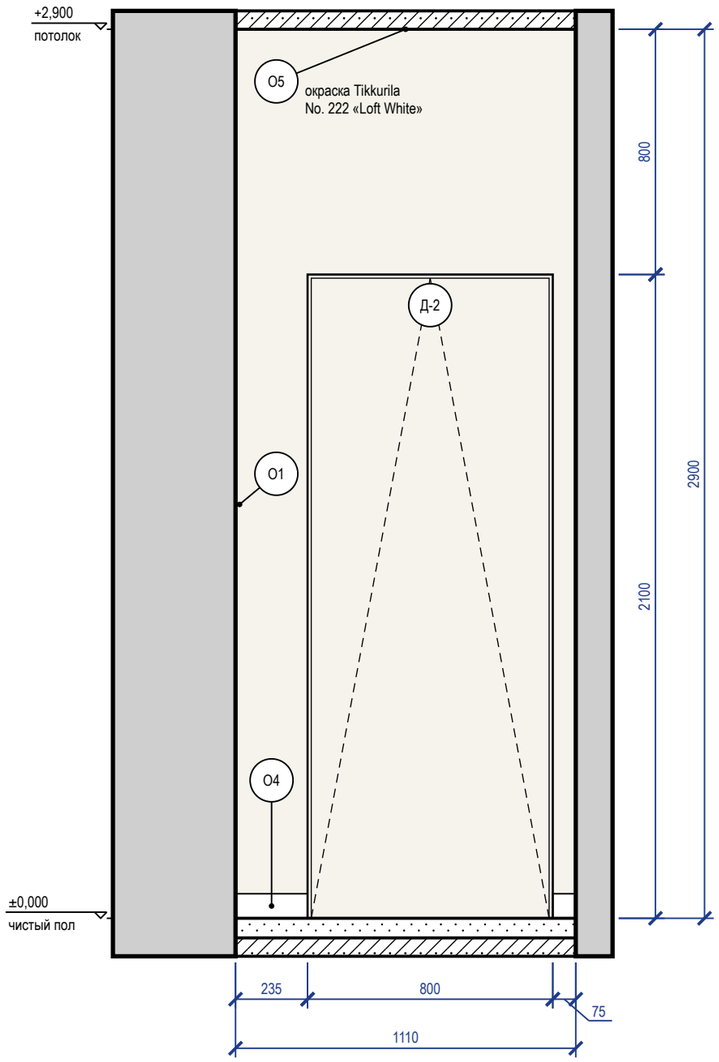

Развёртка стены Г2


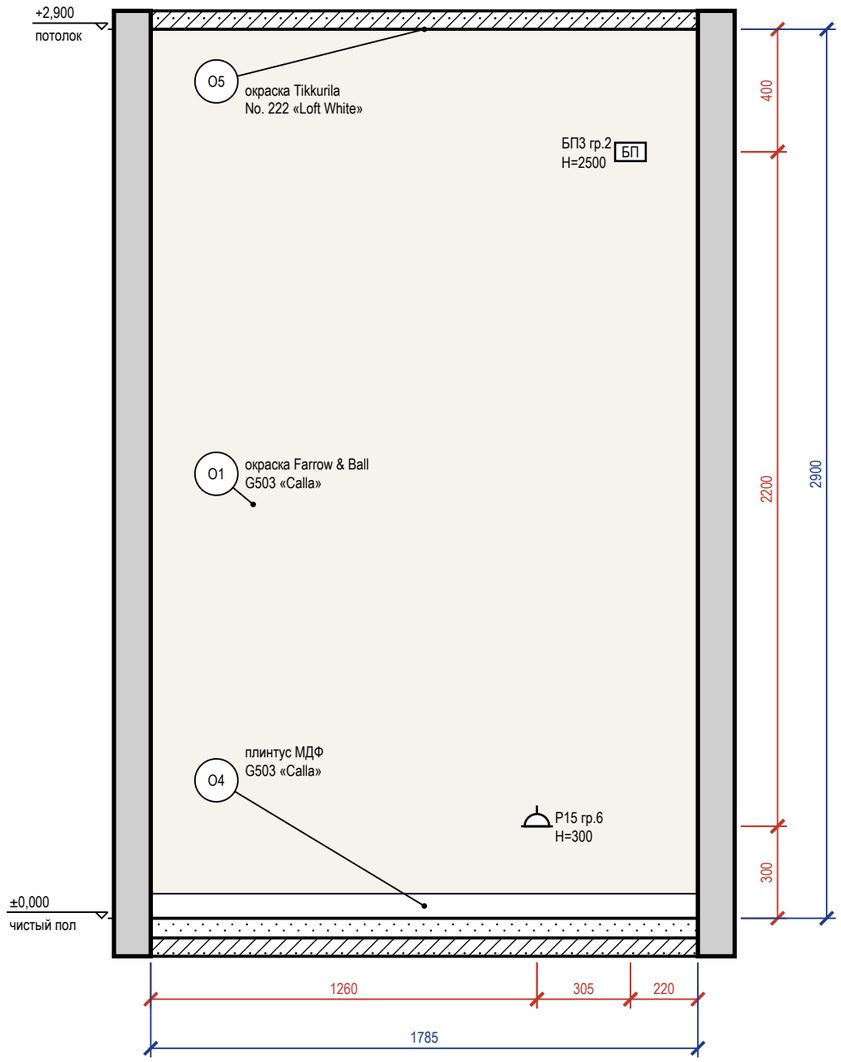


Схема развёрток (М 1:100)

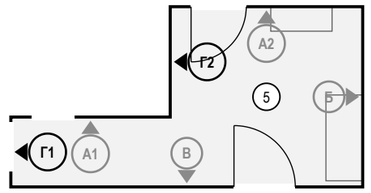

Ведомость отделки (на листе)

Марка	Поверхность	Материал, изделие	Цвет, код	Кол.
О1	стены	окраска, Farrow & Ball Modern Emulsion, матовая, подготовка Q3	Tikkurila G503 «Calla»	6,7 м²
О4	плинтус	плинтус МДФ, h 80 мм, аналог: плинтус МДФ под покраску 80×16	Tikkurila G503 «Calla»	2,1 м
О5	потолок	окраска, Tikkurila Anti-Reflex 2, глубокоматовая, подготовка Q3	Little Greene No. 222 «Loft White»	12,2 м²

Визуализация этой стены



Примечания

1. Размеры — в мм от чистовых поверхностей стен; условные обозначения и общие указания — лист 2.
2. Двери скрытого монтажа — полотно в плоскости стены, отделка стены по полотну, плинтус прерывается у короба (узел — на листе узлов).

					Проект: Дом 120 м²
	Лист	№ док.	Подпись	Дата	Развёртки стен Г1, Г2. Прихожая (пом. 5)
Дизайнер	Кырлан А.С.			19.10.26	

Стадия	Лист	Листов
П	79	128

выпуск 19.10.2026 № 66b2a77b4d · стр. 79 из 128



					Проект: Дом 120 м²
	Лист	№ док.	Подпись	Дата	Визуализация: Спальня родителей
Дизайнер	Кырлан А.С.			19.10.26	

Стадия	Лист	Листов
П	80	128

выпуск 19.10.2026 № 66b2a77b4d · стр. 80 из 128



					Проект: Дом 120 м²	
	Лист	№ док.	Подпись	Дата	Визуализация: Спальня родителей	Стадия / Лист / Листов
Дизайнер	Кырлан А.С.			19.10.26		П / 81 / 128

выпуск 19.10.2026 № 66b2a77b4d · стр. 81 из 128

Развёртка стены А


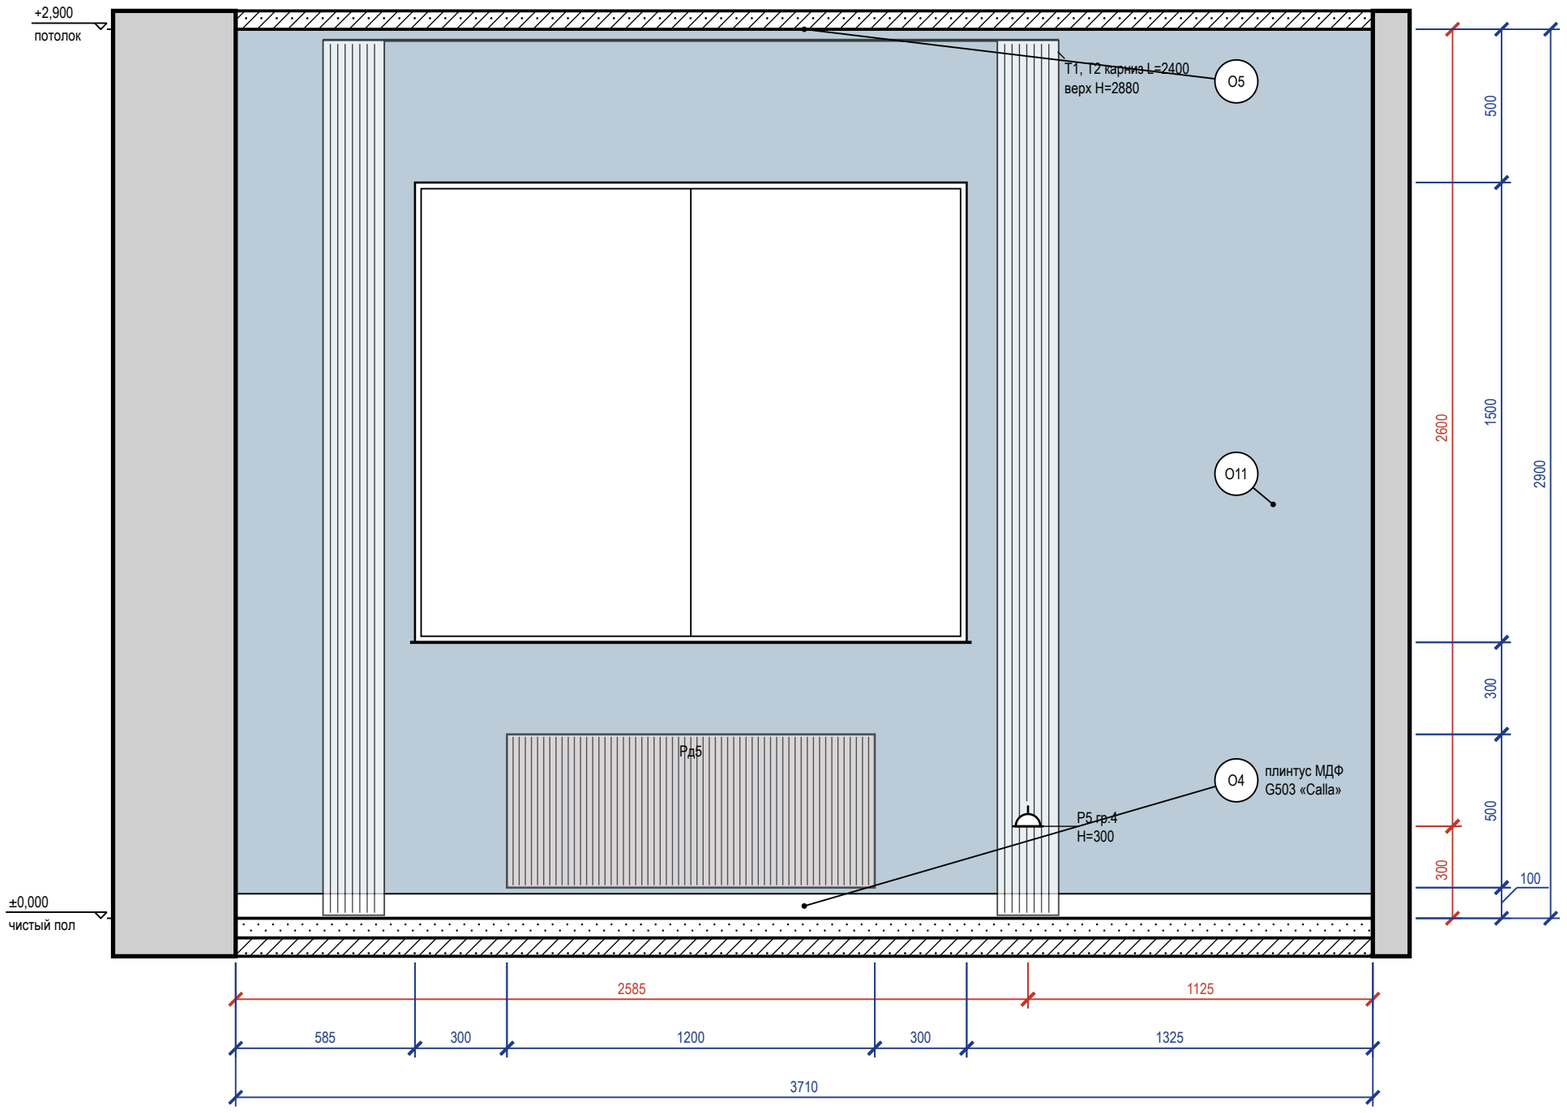


Схема развёрток (М 1:100)

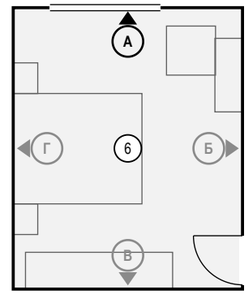

Ведомость отделки (на листе)

Марка	Поверхность	Материал, изделие	Цвет, код	Кол.
О4	плинтус	плинтус МДФ, h 80 мм, аналог: плинтус МДФ под покраску 80×16	Tikkurila G503 «Calla»	3,7 м
О5	потолок	окраска, Tikkurila Anti-Reflex 2, глубокоматовая, подготовка Q3	Little Greene No. 222 «Loft White»	17,2 м²
О11	акцентная стена	окраска, Farrow & Ball Modern Emulsion, матовая, подготовка Q3	Farrow & Ball No. 89 «Lulworth Blue — светлая морская лазурь»	8,1 м²

Визуализация этой стены



Примечания

1. Размеры — в мм от чистовых поверхностей стен; условные обозначения и общие указания — лист 2.
2. Карнизы (шины) — по ведомости текстиля декоратора; длина L и верх H — по развёртке, крепление — до окраски потолка.
3. Линии узора (швы плитки, складки штор, рёбра радиаторов) прерываются у знаков и выносок — просвет между линиями не менее 0,7 мм.

					Проект: Дом 120 м²
	Лист	№ док.	Подпись	Дата	Развёртка стены А. Спальня родителей (пом. 6)
Дизайнер	Кырлан А.С.			19.10.26	

Стадия	Лист	Листов
П	82	128

выпуск 19.10.2026 № 66b2a77b4d · стр. 82 из 128

Развёртка стены Б


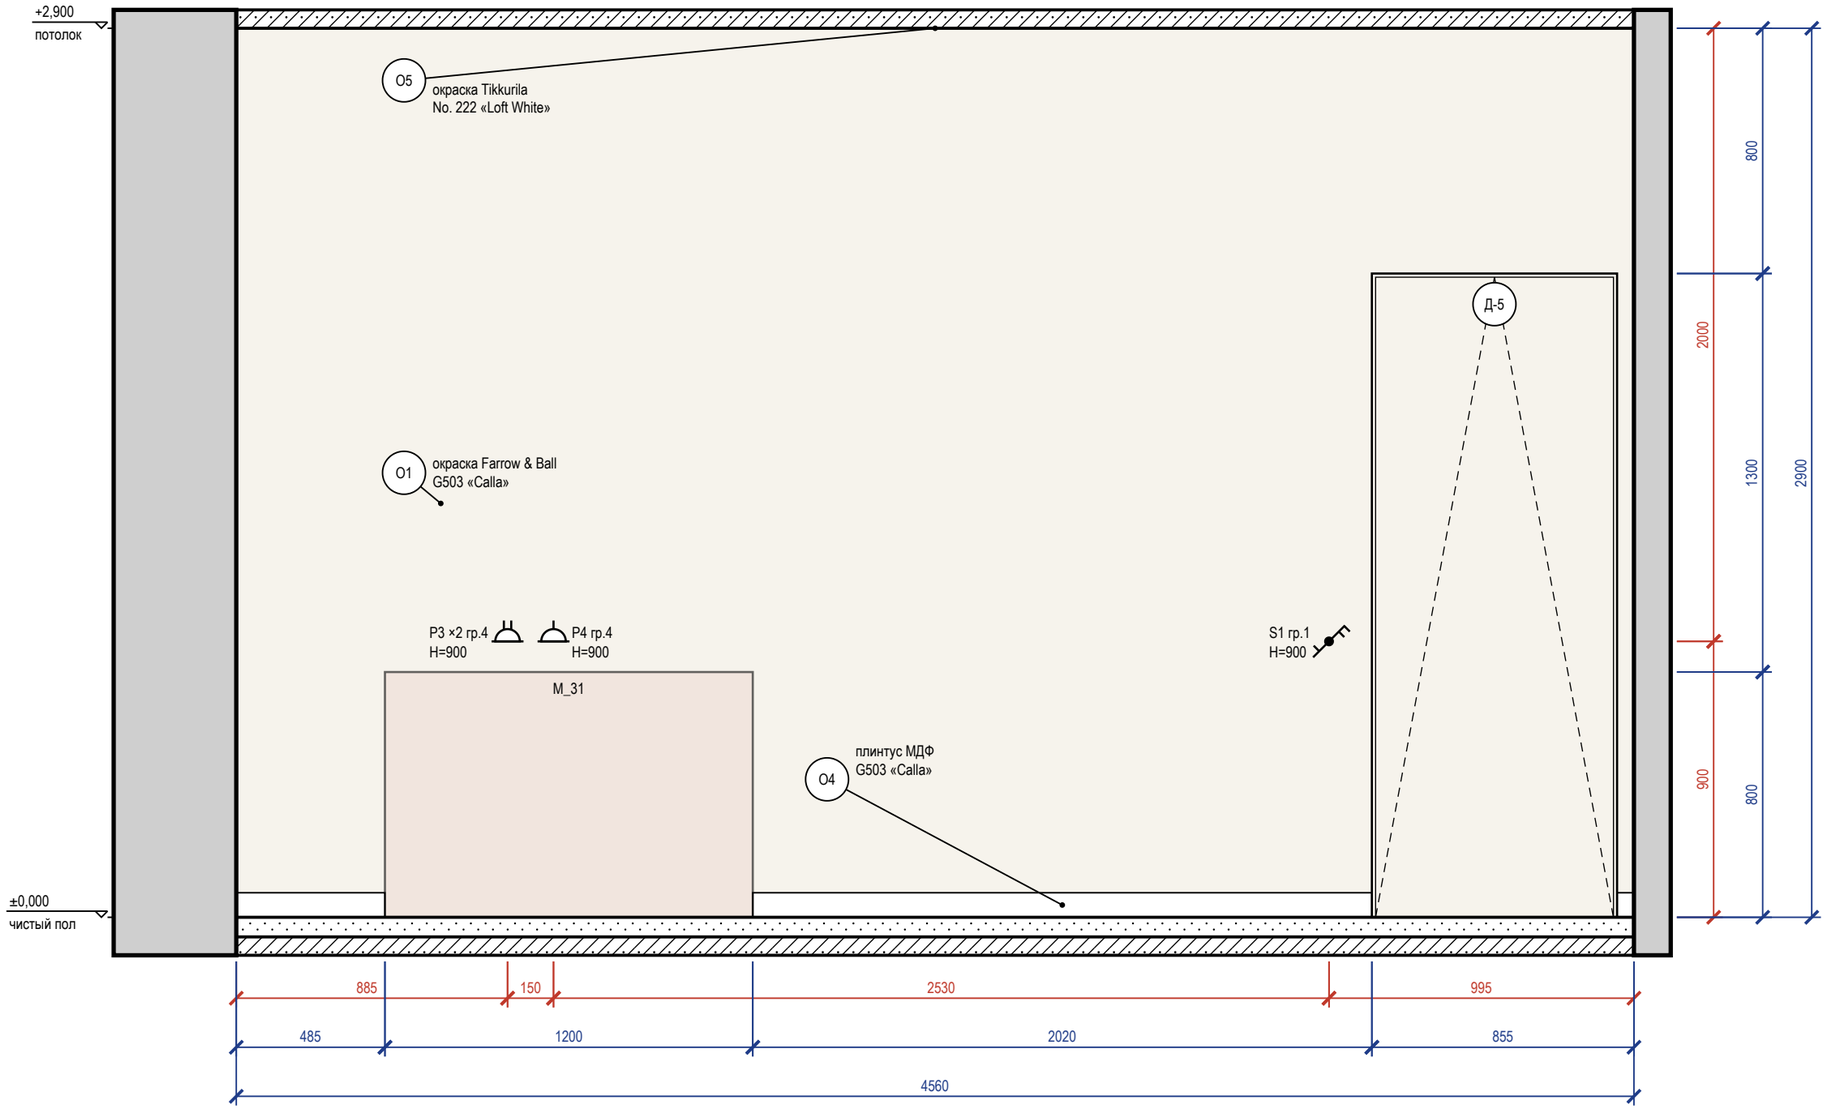


Схема развёрток (М 1:100)

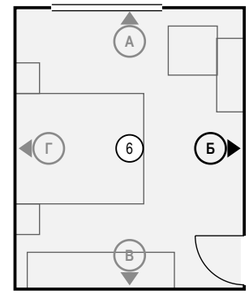

Ведомость отделки (на листе)

Марка	Поверх ность	Материал, изделие	Цвет, код	Кол.
О1	стены	окраска, Farrow & Ball Modern Emulsion, матовая, подготовка Q3	Tikkurila G503 «Calla»	11,5 м²
О4	плинтус	плинтус МДФ, h 80 мм, аналог: плинтус МДФ под покраску 80×16	Tikkurila G503 «Calla»	2,6 м
О5	потолок	окраска, Tikkurila Anti-Reflex 2, глубокоматовая, подготовка Q3	Little Greene No. 222 «Loft White»	17,2 м²

Примечания

1. Размеры — в мм от чистовых поверхностей стен; условные обозначения и общие указания — лист 2.
2. Двери скрытого монтажа — полотно в плоскости стены, отделка стены по полотну, плинтус прерывается у короба (узел — на листе узлов).

					Проект: Дом 120 м²
	Лист	№ док.	Подпись	Дата	Развёртка стены Б. Спальня родителей (пом. 6)
Дизайнер	Кырлан А.С.			19.10.26	

Стадия	Лист	Листов
П	83	128

выпуск 19.10.2026 № 66b2a77b4d · стр. 83 из 128

Развёртка стены В


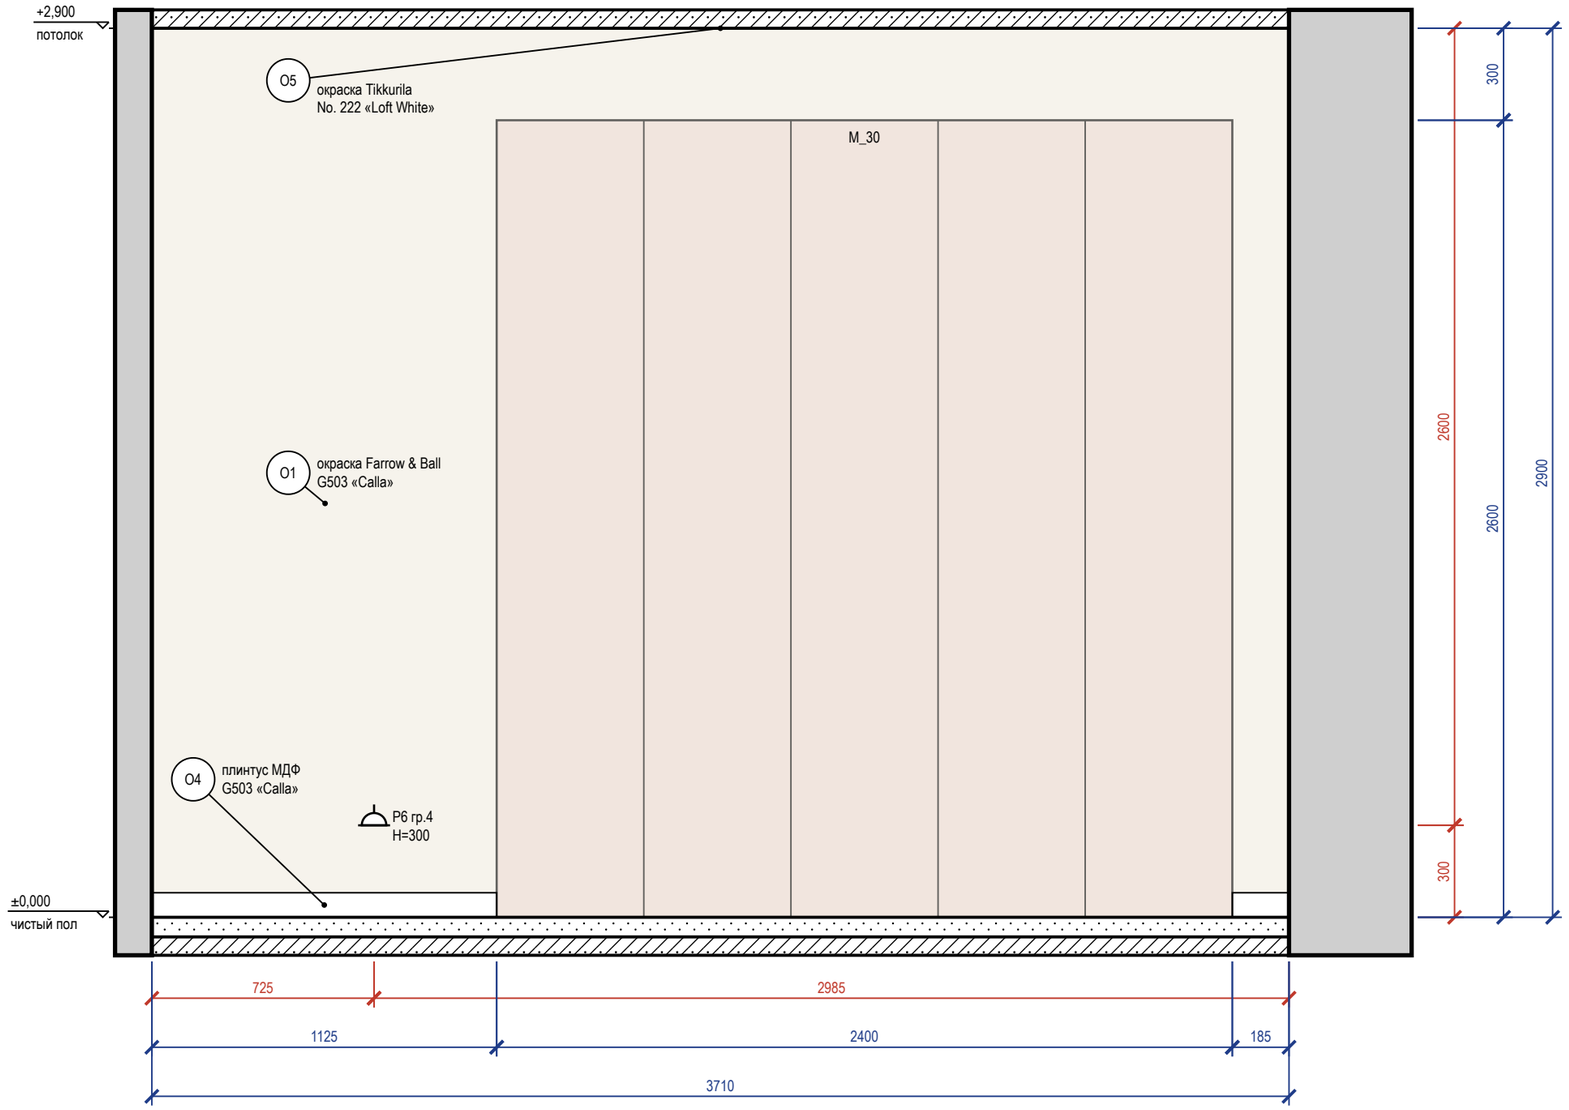


Схема развёрток (М 1:100)

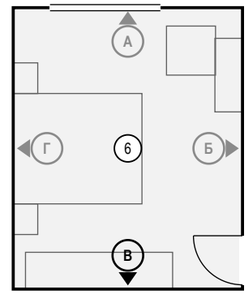

Ведомость отделки (на листе)


Марка	Поверхность	Материал, изделие	Цвет, код	Кол.
О1	стены	окраска, Farrow & Ball Modern Emulsion, матовая, подготовка Q3	Tikkurila G503 «Calla»	10,8 м²
О4	плинтус	плинтус МДФ, h 80 мм, аналог: плинтус МДФ под покраску 80×16	Tikkurila G503 «Calla»	1,3 м
О5	потолок	окраска, Tikkurila Anti-Reflex 2, глубокоматовая, подготовка Q3	Little Greene No. 222 «Loft White»	17,2 м²

Визуализация этой стены — лист 80



5 **Плинтус МДФ 80×16 мм у окрашенной стены (М 1:20)**

Узел 5 — лист С3

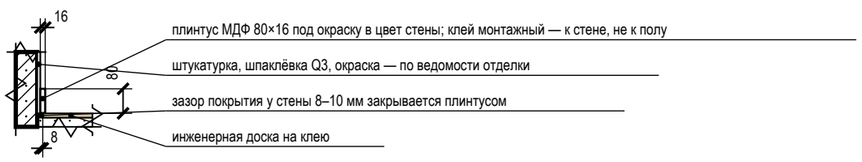

Примечания

1. Размеры — в мм от чистовых поверхностей стен; условные обозначения и общие указания — лист 2.

					Проект: Дом 120 м²
	Лист	№ док.	Подпись	Дата	Развёртка стены В. Спальня родителей (пом. 6)
Дизайнер	Кырлан А.С.			19.10.26	

Стадия	Лист	Листов
П	84	128

выпуск 19.10.2026 № 66b2a77b4d · стр. 84 из 128

Развёртка стены Г


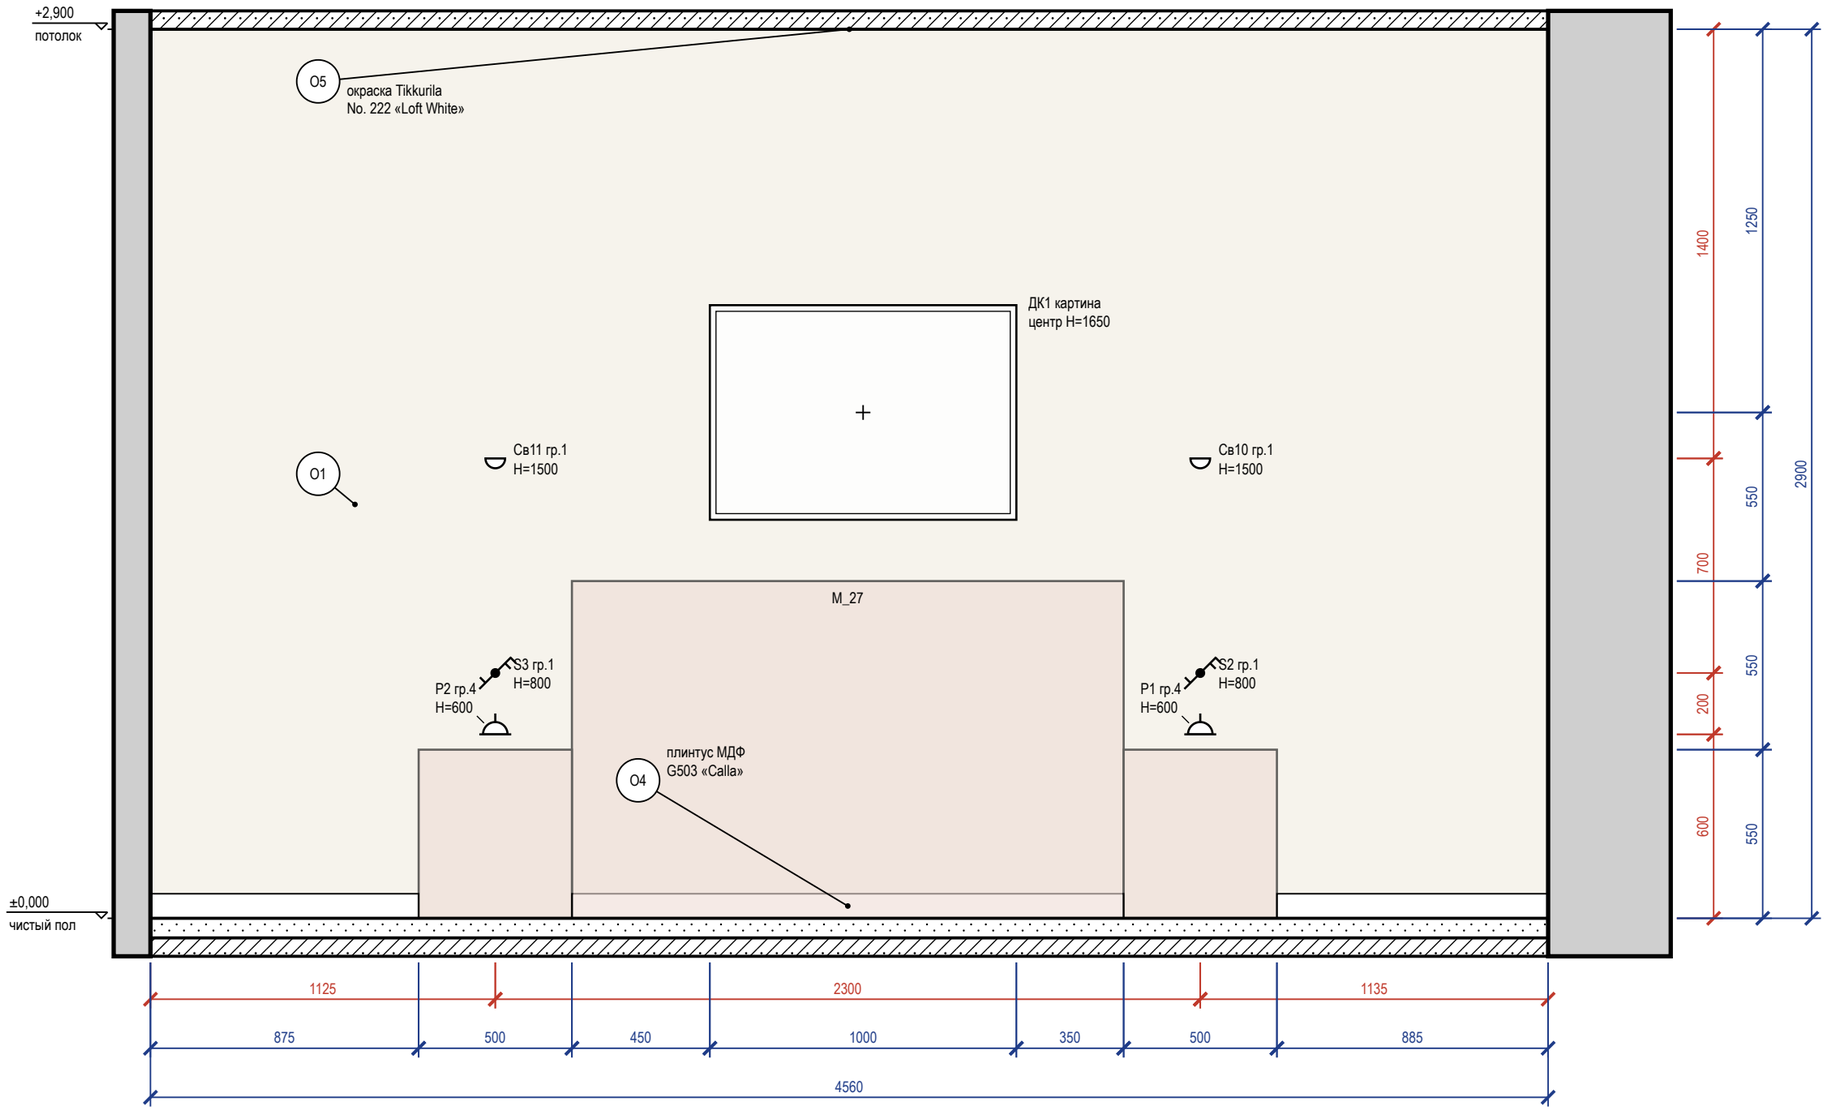


Схема развёрток (М 1:100)

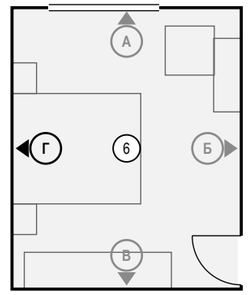

Ведомость отделки (на листе)

Марка	Поверхность	Материал, изделие	Цвет, код	Кол.
О1	стены	окраска, Farrow & Ball Modern Emulsion, матовая, подготовка Q3	Tikkurila G503 «Calla»	13,2 м²
О4	плинтус	плинтус МДФ, h 80 мм, аналог: плинтус МДФ под покраску 80×16	Tikkurila G503 «Calla»	3,6 м
О5	потолок	окраска, Tikkurila Anti-Reflex 2, глубокоматовая, подготовка Q3	Little Greene No. 222 «Loft White»	17,2 м²

Примечания

1. Размеры — в мм от чистовых поверхностей стен; условные обозначения и общие указания — лист 2.
2. Картины и зеркала крепить к основанию по паспорту изделия (закладные и анкеры — в перечне скрытых работ); крест — ось центра предмета.

					Проект: Дом 120 м²
	Лист	№ док.	Подпись	Дата	Развёртка стены Г. Спальня родителей (пом. 6)
Дизайнер	Кырлан А.С.			19.10.26	

Стадия	Лист	Листов
П	85	128

выпуск 19.10.2026 № 66b2a77b4d · стр. 85 из 128



					Проект: Дом 120 м²
	Лист	№ док.	Подпись	Дата	Визуализация детской
Дизайнер	Кырлан А.С.			19.10.26	

Стадия	Лист	Листов
П	86	128

выпуск 19.10.2026 № 66b2a77b4d · стр. 86 из 128



					Проект: Дом 120 м²	
	Лист	№ док.	Подпись	Дата	Визуализация детской	Стадия / Лист / Листов
Дизайнер	Кырлан А.С.			19.10.26		П / 87 / 128

выпуск 19.10.2026 № 66b2a77b4d · стр. 87 из 128

Развёртка стены А


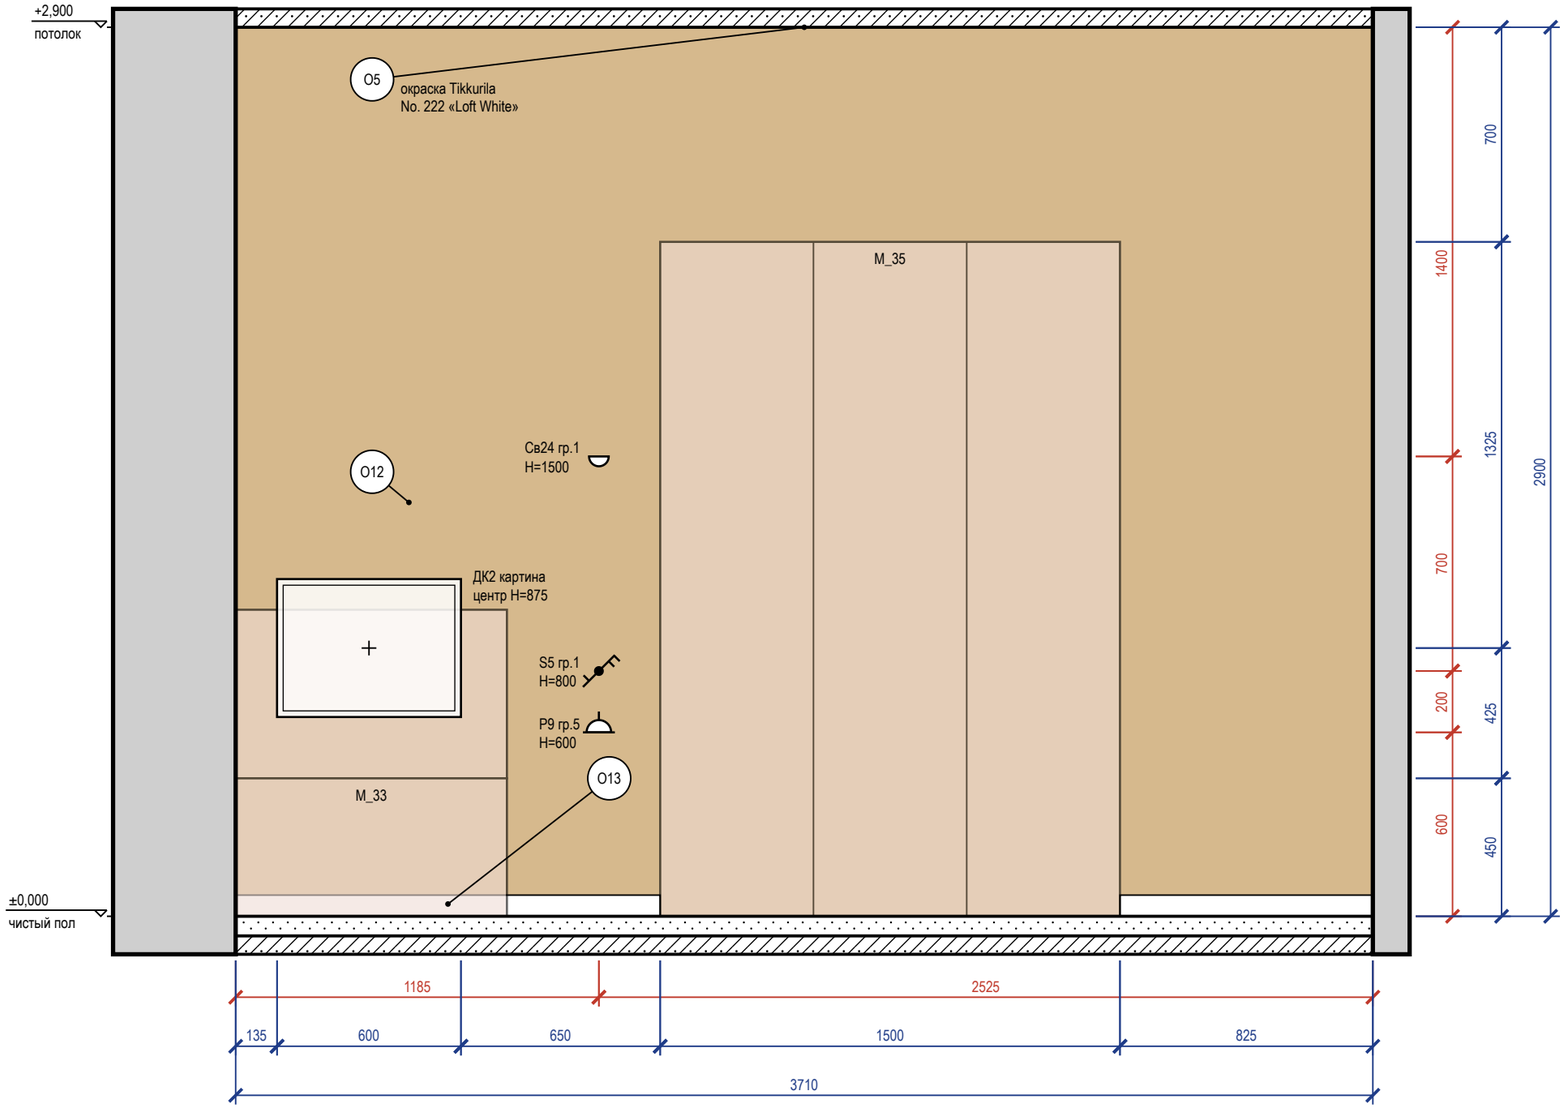


Схема развёрток (М 1:100)

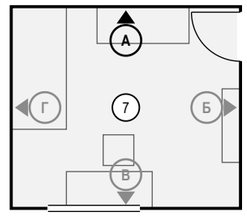

Ведомость отделки (на листе)

Марка	Поверхность	Материал, изделие	Цвет, код	Кол.
О5	потолок	окраска, Tikkurila Anti-Reflex 2, глубокоматовая, подготовка Q3	Little Greene No. 222 «Loft White»	12,3 м²
О12	акцентная стена	окраска, Farrow & Ball Modern Emulsion, матовая, подготовка Q3	Farrow & Ball No. 66 «India Yellow — охра / горчица итальянских фасадов»	10,8 м²
О13	плинтус	плинтус МДФ, Orac Decor Contour (Luxxus), h 69 мм, SX165	Tikkurila G503 «Calla»	2,2 м

Визуализация этой стены — лист 86



Примечания

1. Размеры — в мм от чистовых поверхностей стен; условные обозначения и общие указания — лист 2.
2. Картины и зеркала крепить к основанию по паспорту изделия (закладные и анкеры — в перечне скрытых работ); крест — ось центра предмета.

	Лист	№ док.	Подпись	Дата
Дизайнер	Кырлан А.С.			19.10.26

Проект: Дом 120 м²

Развёртка стены А. Детская (пом. 7)

Стадия	Лист	Листов
П	88	128

выпуск 19.10.2026 № 66b2a77b4d · стр. 88 из 128

Развёртка стены Б


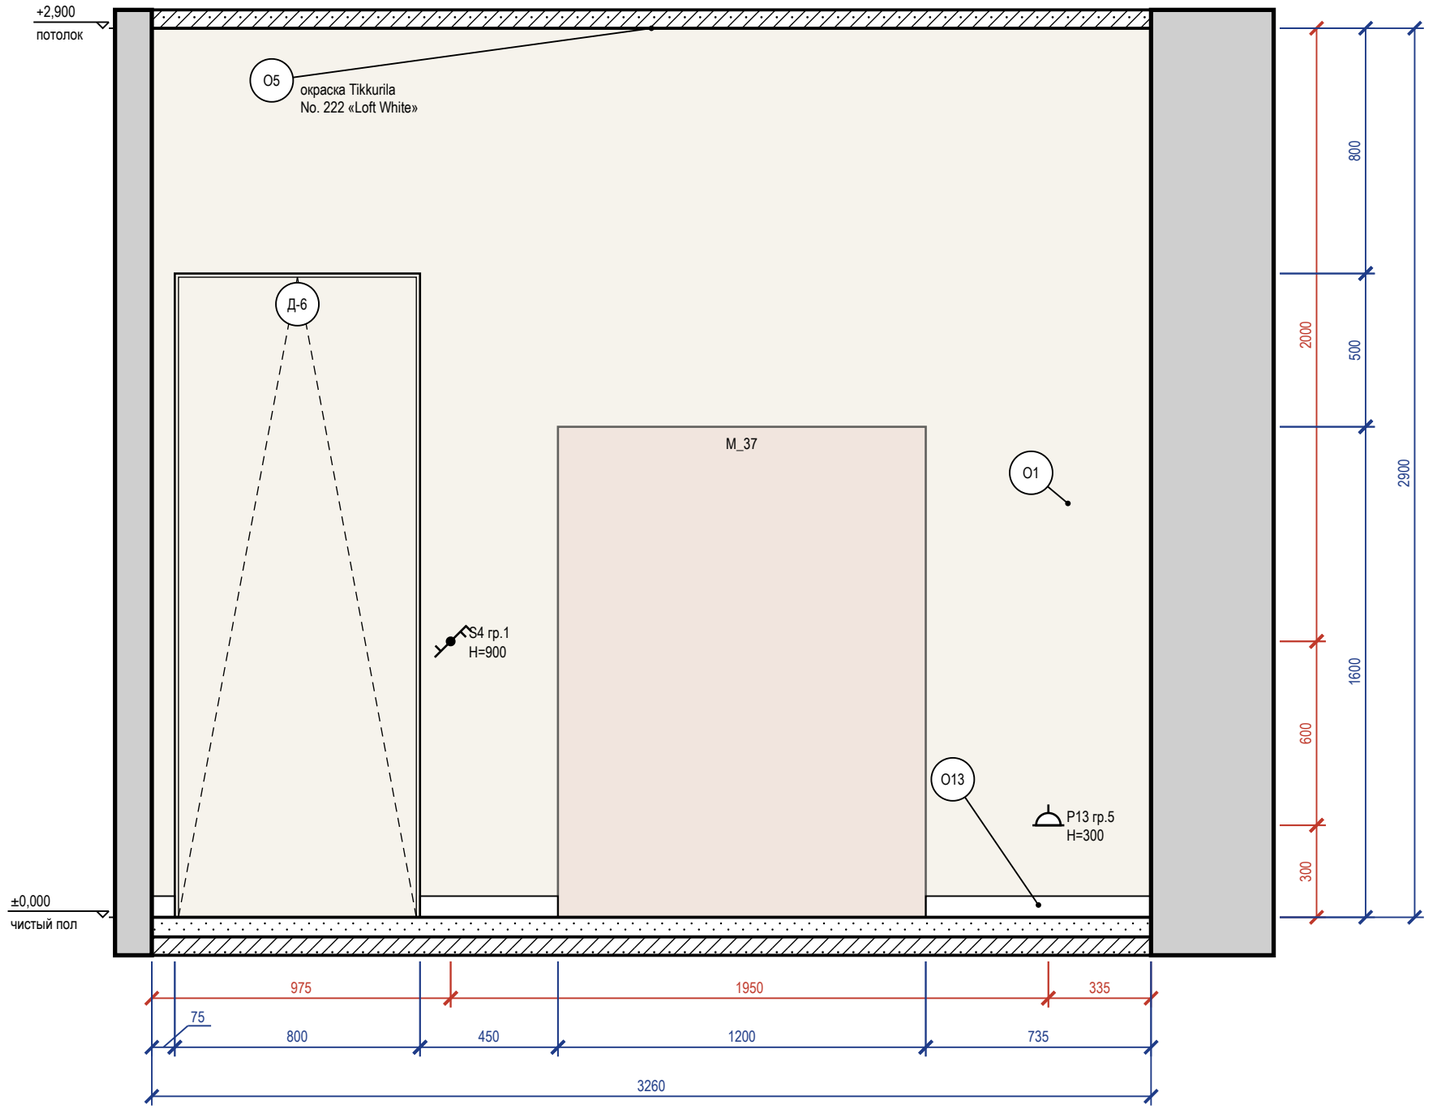


Схема развёрток (М 1:100)

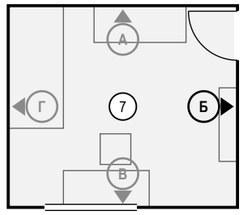

Ведомость отделки (на листе)

Марка	Поверхность	Материал, изделие	Цвет, код	Кол.
О1	стены	окраска, Farrow & Ball Modern Emulsion, матовая, подготовка Q3	Tikkurila G503 «Calla»	7,8 м²
О5	потолок	окраска, Tikkurila Anti-Reflex 2, глубокоматовая, подготовка Q3	Little Greene No. 222 «Loft White»	12,3 м²
О13	плинтус	плинтус МДФ, Orac Decor Contour (Luxxus), h 69 мм, SX165	Tikkurila G503 «Calla»	1,3 м

Примечания

1. Размеры — в мм от чистовых поверхностей стен; условные обозначения и общие указания — лист 2.
2. Двери скрытого монтажа — полотно в плоскости стены, отделка стены по полотну, плинтус прерывается у короба (узел — на листе узлов).

					Проект: Дом 120 м²
	Лист	№ док.	Подпись	Дата	Развёртка стены Б. Детская (пом. 7)
Дизайнер	Кырлан А.С.			19.10.26	

Стадия	Лист	Листов
П	89	128

выпуск 19.10.2026 № 66b2a77b4d · стр. 89 из 128

Развёртка стены В


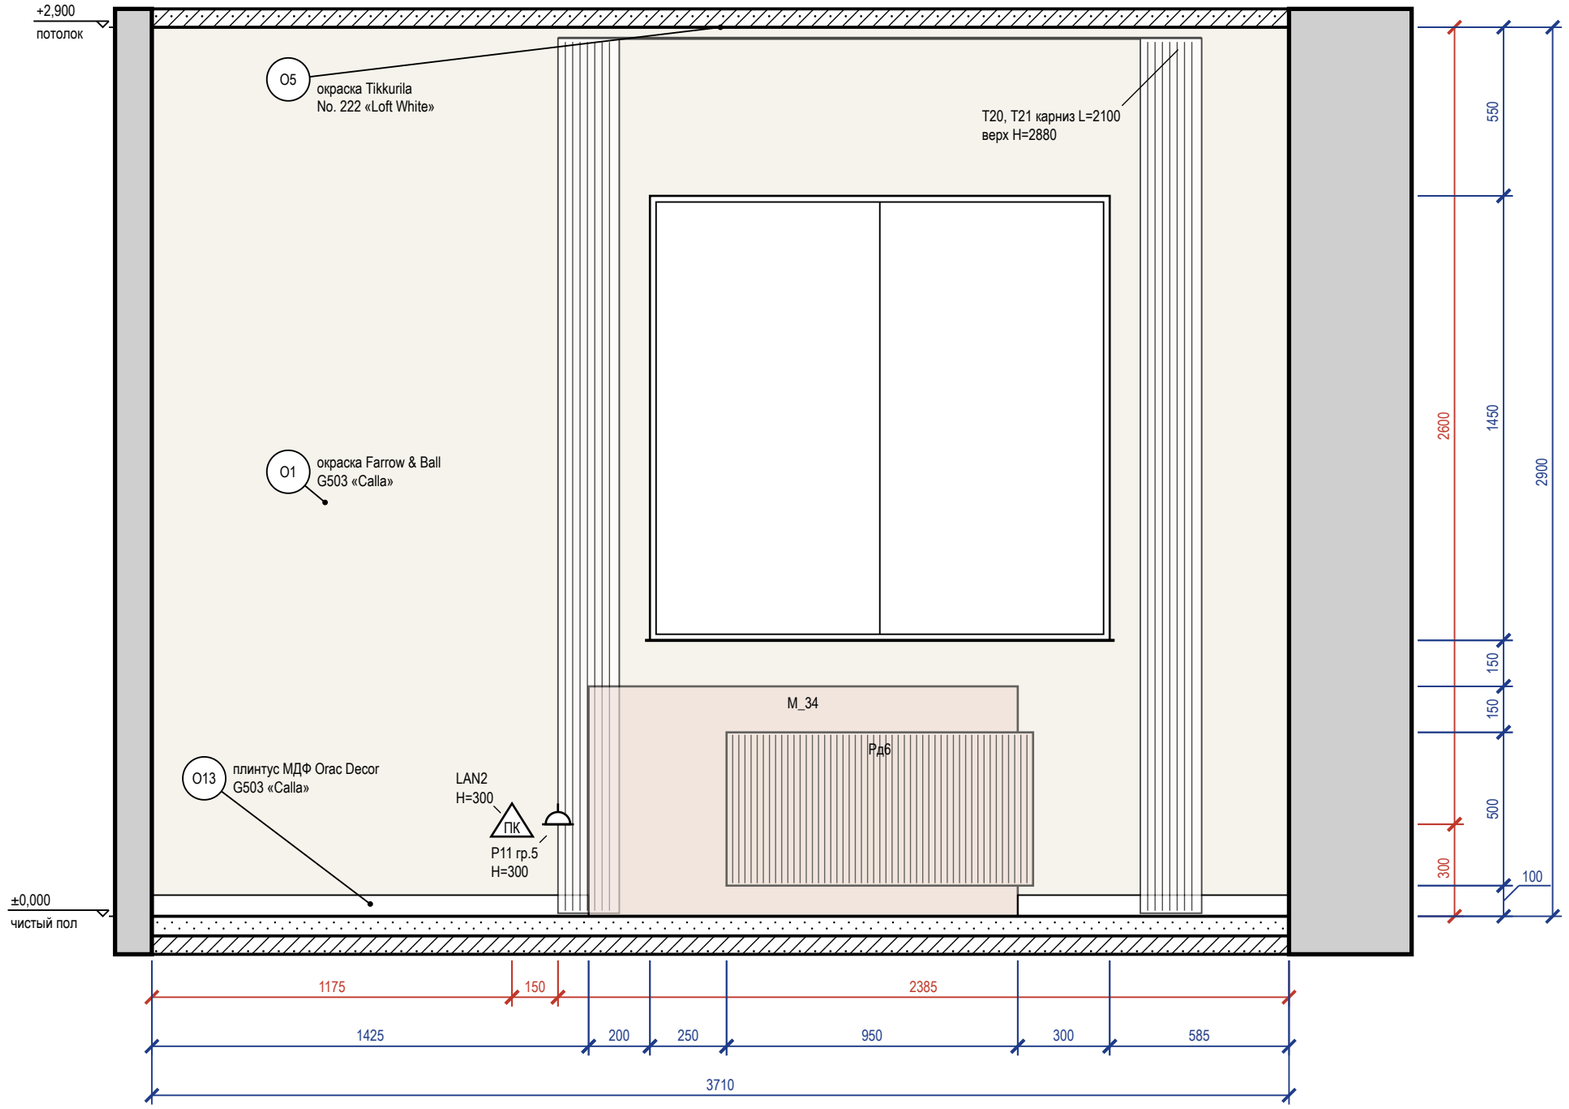



Схема развёрток (М 1:100)

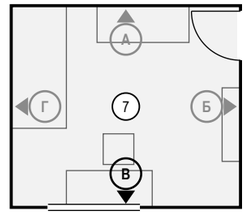

Ведомость отделки (на листе)

Марка	Поверхность	Материал, изделие	Цвет, код	Кол.
О1	стены	окраска, Farrow & Ball Modern Emulsion, матовая, подготовка Q3	Tikkurila G503 «Calla»	8,6 м²
О5	потолок	окраска, Tikkurila Anti-Reflex 2, глубокоматовая, подготовка Q3	Little Greene No. 222 «Loft White»	12,3 м²
О13	плинтус	плинтус МДФ, Orac Decor Contour (Luxxus), h 69 мм, SX165	Tikkurila G503 «Calla»	2,3 м

Визуализация этой стены

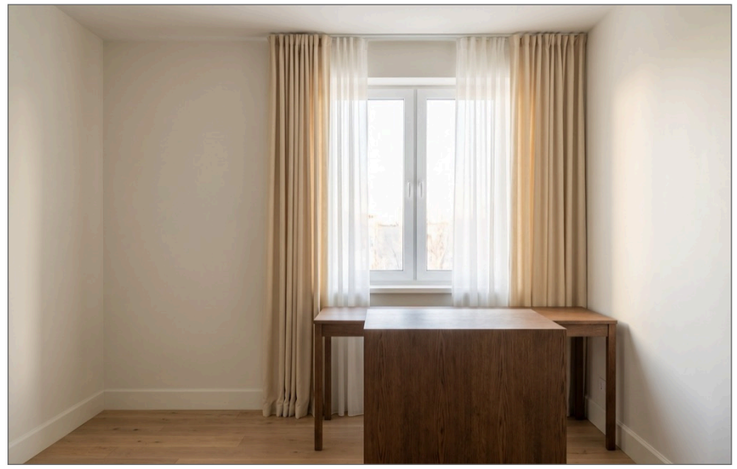

Примечания

1. Размеры — в мм от чистовых поверхностей стен; условные обозначения и общие указания — лист 2.
2. Карнизы (шины) — по ведомости текстиля декоратора; длина L и верх H — по развёртке, крепление — до окраски потолка.

					Проект: Дом 120 м²
	Лист	№ док.	Подпись	Дата	Развёртка стены В. Детская (пом. 7)
Дизайнер	Кырлан А.С.			19.10.26	

Стадия	Лист	Листов
П	90	128

выпуск 19.10.2026 № 66b2a77b4d · стр. 90 из 128

Развёртка стены Г


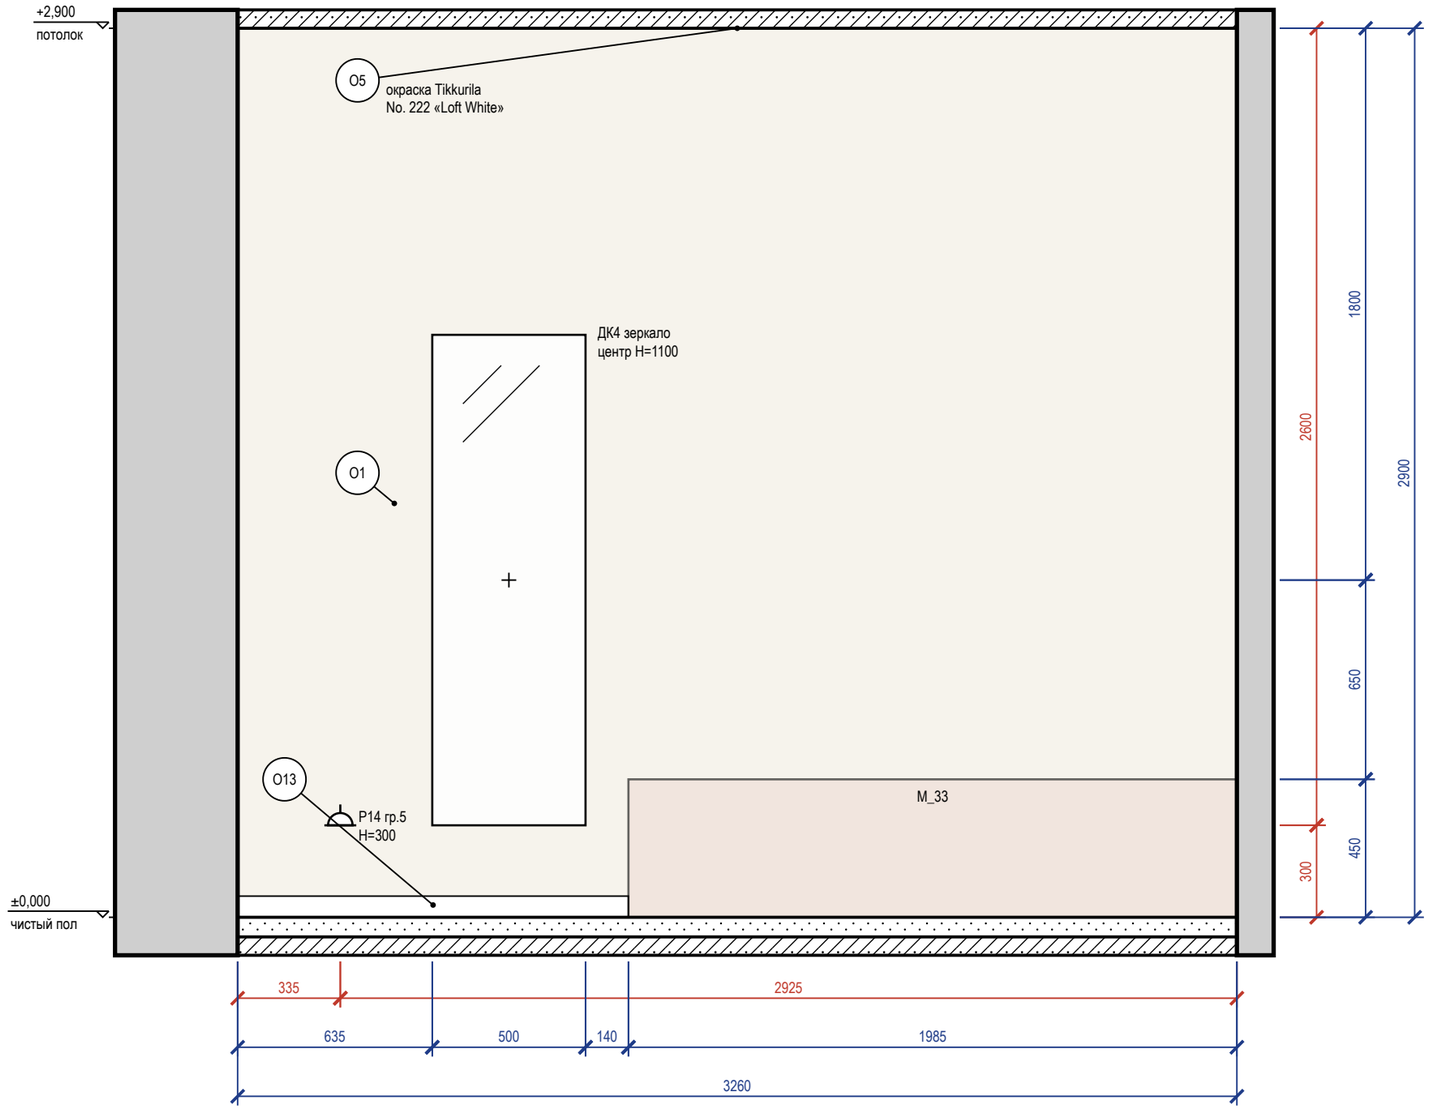


Схема развёрток (М 1:100)

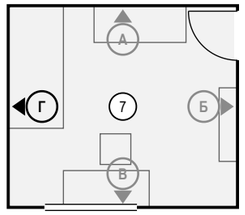

Ведомость отделки (на листе)

Марка	Поверхность	Материал, изделие	Цвет, код	Кол.
О1	стены	окраска, Farrow & Ball Modern Emulsion, матовая, подготовка Q3	Tikkurila G503 «Calla»	9,5 м²
О5	потолок	окраска, Tikkurila Anti-Reflex 2, глубокоматовая, подготовка Q3	Little Greene No. 222 «Loft White»	12,3 м²
О13	плинтус	плинтус МДФ, Orac Decor Contour (Luxxus), h 69 мм, SX165	Tikkurila G503 «Calla»	1,3 м

Примечания

1. Размеры — в мм от чистовых поверхностей стен; условные обозначения и общие указания — лист 2.
2. Картины и зеркала крепить к основанию по паспорту изделия (закладные и анкеры — в перечне скрытых работ); крест — ось центра предмета.

					Проект: Дом 120 м²
	Лист	№ док.	Подпись	Дата	Развёртка стены Г. Детская (пом. 7)
Дизайнер	Кырлан А.С.			19.10.26	

Стадия	Лист	Листов
П	91	128

выпуск 19.10.2026 № 66b2a77b4d · стр. 91 из 128




					Проект: Дом 120 м²
	Лист	№ док.	Подпись	Дата	
Дизайнер	Кырлан А.С.			19.10.26	Визуализация гардеробной

Стадия	Лист	Листов
П	92	128

выпуск 19.10.2026 № 66b2a77b4d · стр. 92 из 128

Развёртка стены А

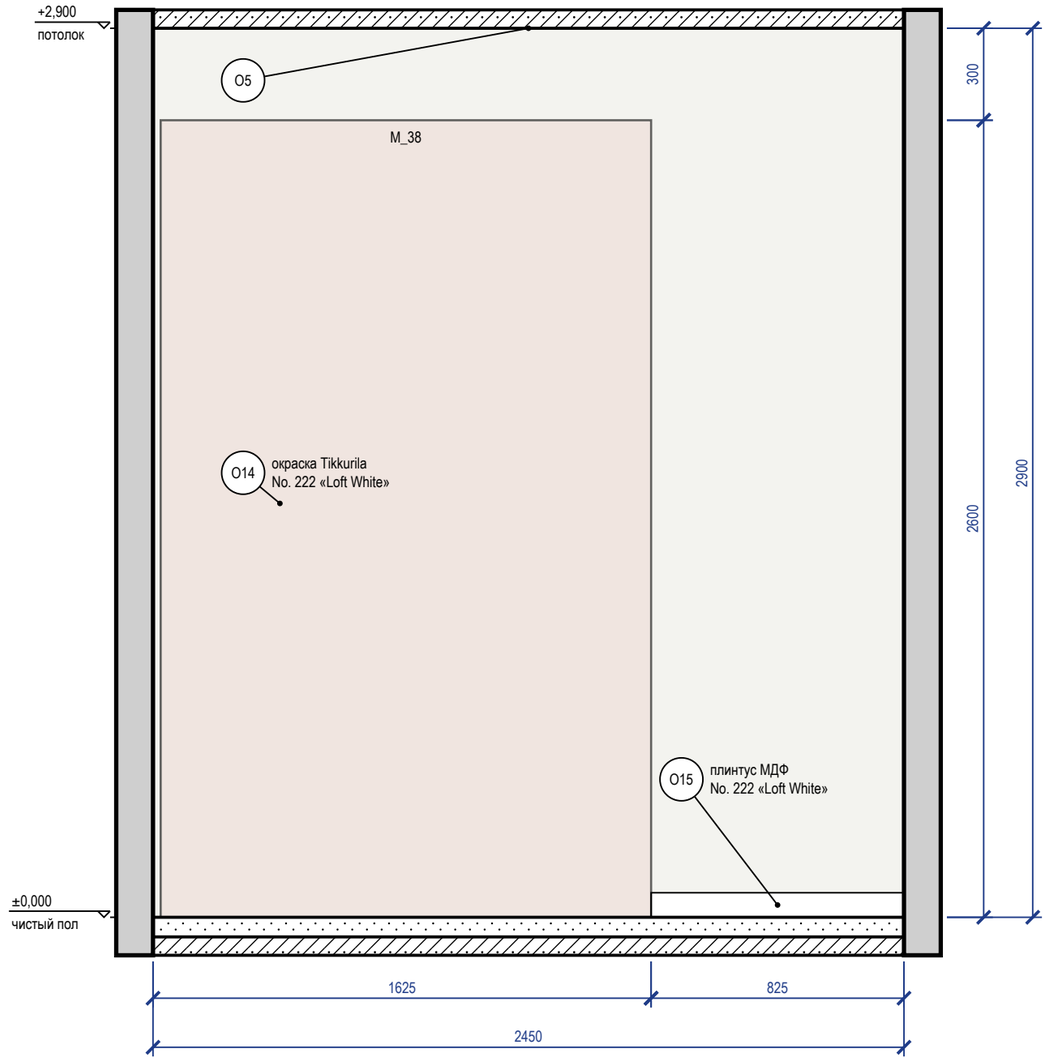

Развёртка стены Б


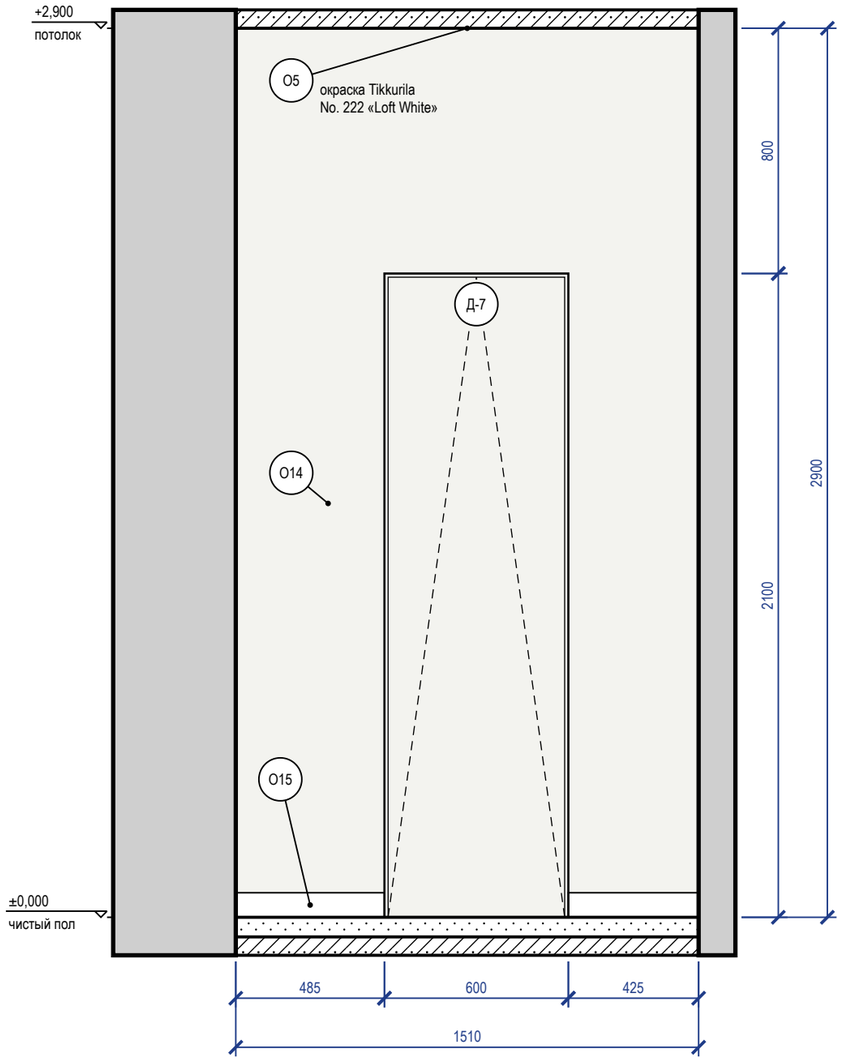


Схема развёрток (М 1:100)

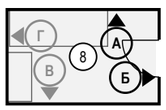

Ведомость отделки (на листе)

Марка	Поверхность	Материал, изделие	Цвет, код	Кол.
О5	потолок	окраска, Tikkurila Anti-Reflex 2, глубокоматовая, подготовка Q3	Little Greene No. 222 «Loft White»	3,8 м²
О14	стены	окраска, Tikkurila Harmony, матовая, подготовка Q3	Little Greene No. 222 «Loft White»	10,2 м²
О15	плинтус	плинтус МДФ, h 80 мм, аналог: плинтус МДФ под покраску 80×16	Little Greene No. 222 «Loft White»	1,7 м

Визуализация этой стены



Примечания

1. Размеры — в мм от чистовых поверхностей стен; условные обозначения и общие указания — лист 2.
2. Двери скрытого монтажа — полотно в плоскости стены, отделка стены по полотну, плинтус прерывается у короба (узел — на листе узлов).

	Лист	№ док.	Подпись	Дата
Дизайнер	Кырлан А.С.			19.10.26


Проект: Дом 120 м²

Развёртки стен А, Б. Гардеробная (пом. 8)

Стадия	Лист	Листов
П	93	128

выпуск 19.10.2026 № 66b2a77b4d · стр. 93 из 128

Развёртка стены В

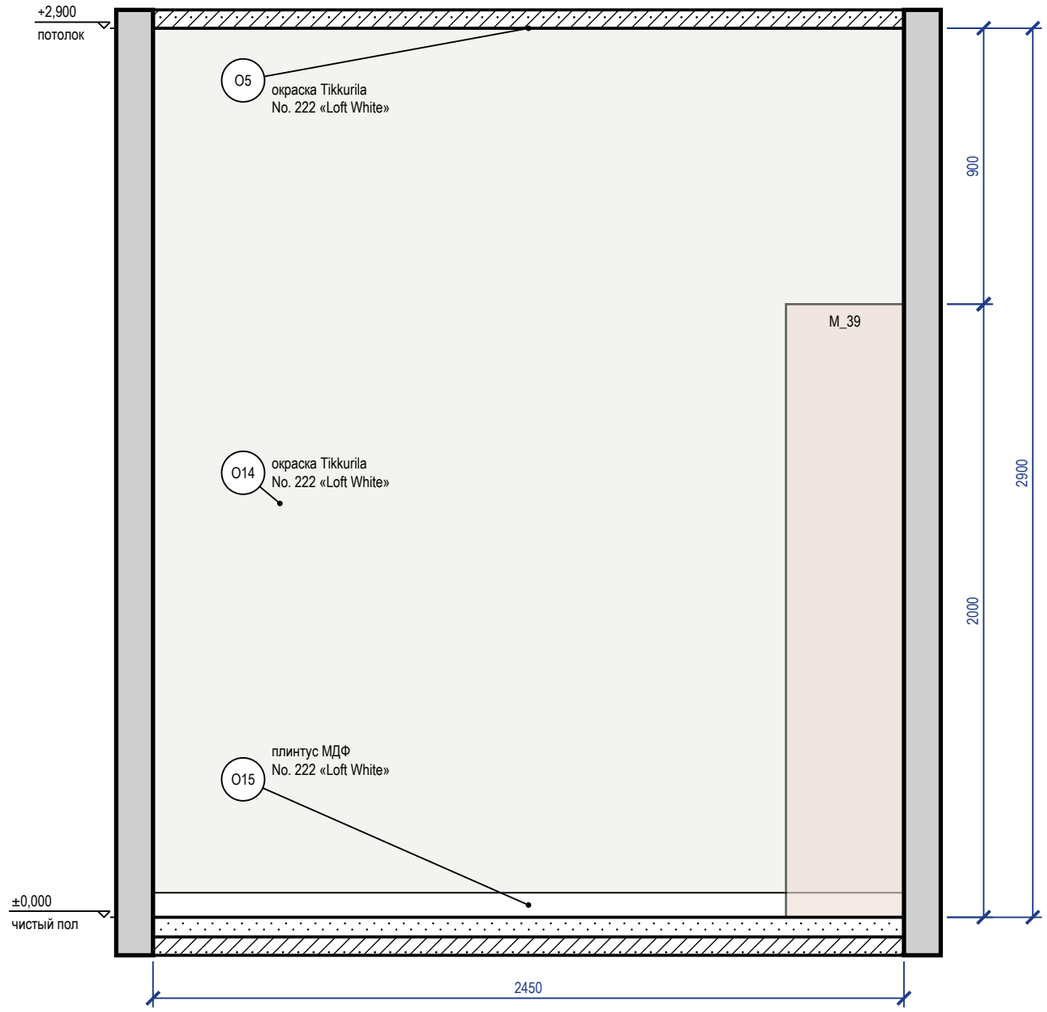

Развёртка стены Г


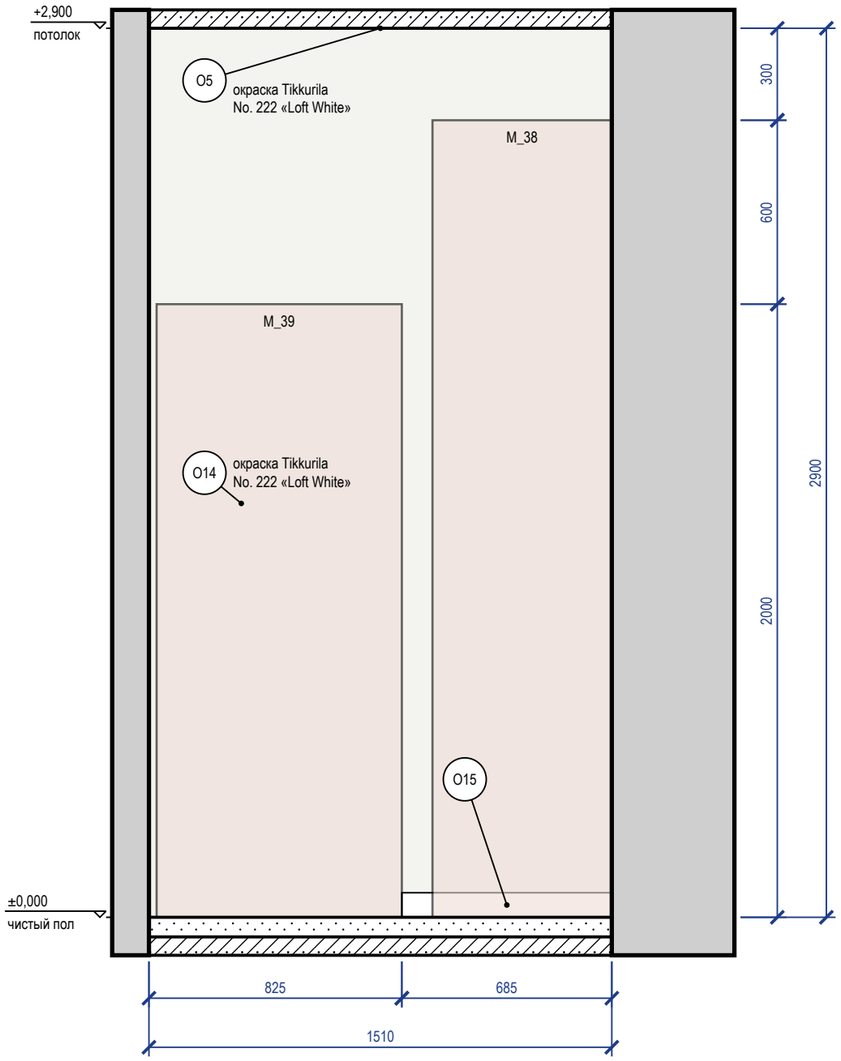



Схема развёрток (М 1:100)

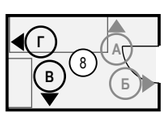

Ведомость отделки (на листе)

Марка	Поверхность	Материал, изделие	Цвет, код	Кол.
О5	потолок	окраска, Tikkurila Anti-Reflex 2, глубокоматовая, подготовка Q3	Little Greene No. 222 «Loft White»	3,8 м²
О14	стены	окраска, Tikkurila Harmony, матовая, подготовка Q3	Little Greene No. 222 «Loft White»	11,5 м²
О15	плинтус	плинтус МДФ, h 80 мм, аналог: плинтус МДФ под покраску 80×16	Little Greene No. 222 «Loft White»	3,1 м

Визуализация этой стены — лист 92

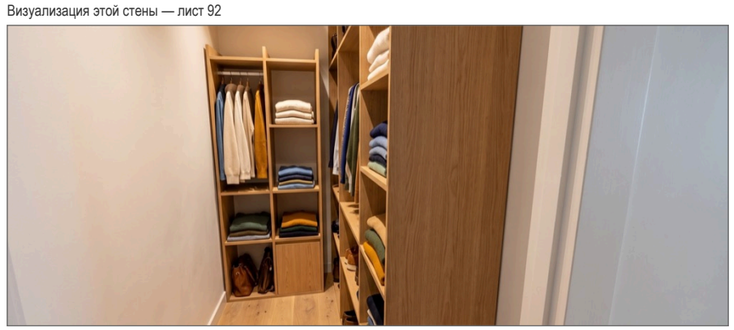

Примечания

1. Размеры — в мм от чистовых поверхностей стен; условные обозначения и общие указания — лист 2.

					Проект: Дом 120 м²
	Лист	№ док.	Подпись	Дата	Развёртки стен В, Г. Гардеробная (пом. 8)
Дизайнер	Кырлан А.С.			19.10.26	

Стадия	Лист	Листов
П	94	128

выпуск 19.10.2026 № 66b2a77b4d · стр. 94 из 128




					Проект: Дом 120 м²
	Лист	№ док.	Подпись	Дата	Визуализация кладовой
Дизайнер	Кырлан А.С.			19.10.26	

Стадия	Лист	Листов
П	95	128

выпуск 19.10.2026 № 66b2a77b4d · стр. 95 из 128

Развёртка стены Б

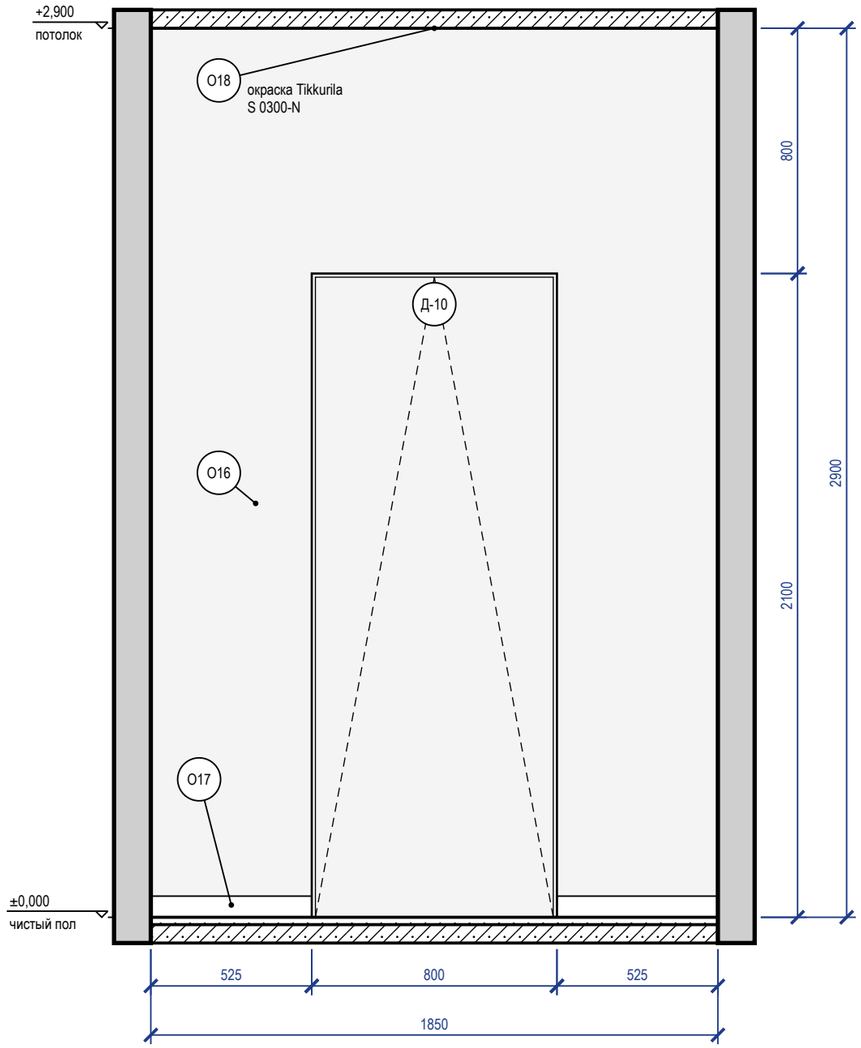

Развёртка стены В


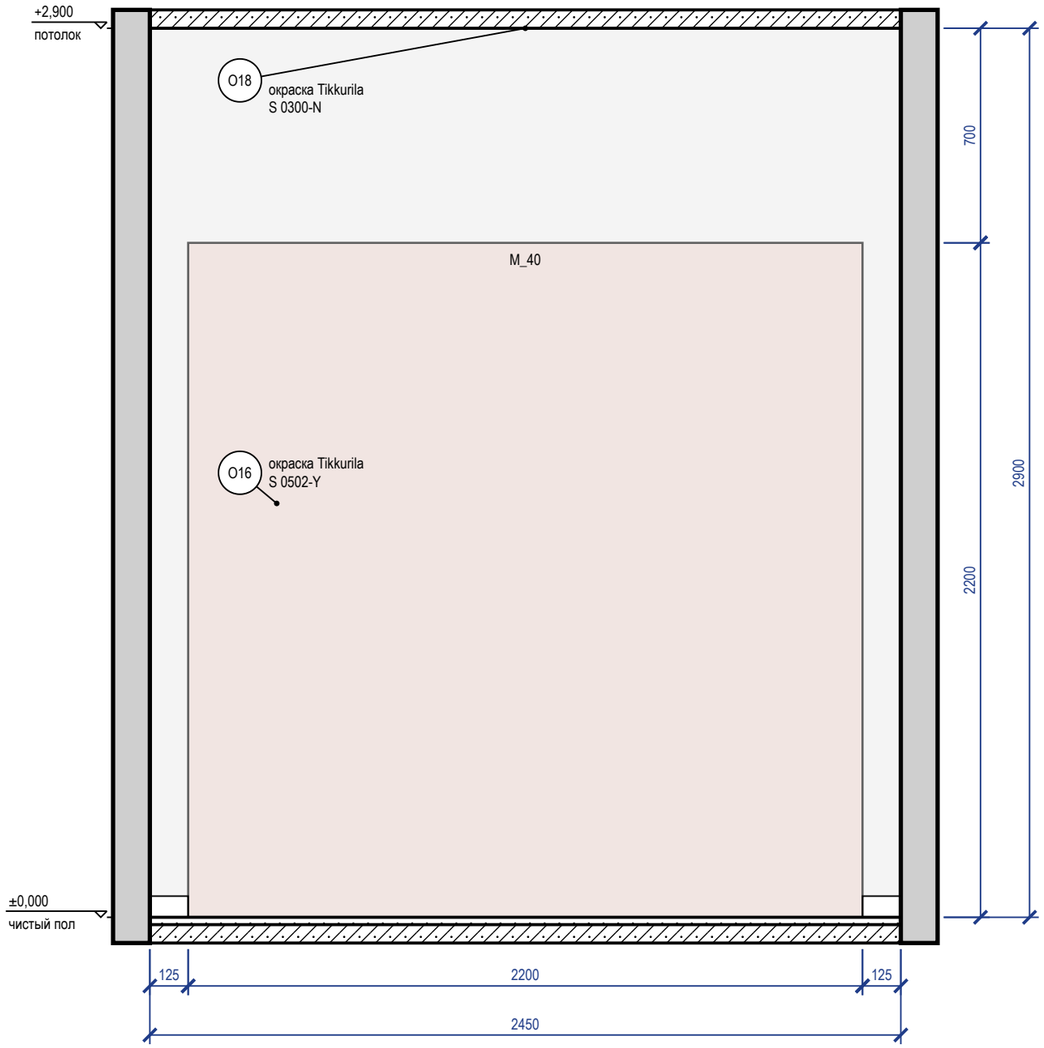


Схема развёрток (М 1:100)

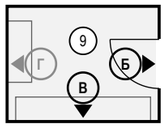

Ведомость отделки (на листе)

Марка	Поверхность	Материал, изделие	Цвет, код	Кол.
О16	стены	окраска, Tikkurila, матовая, подготовка Q3	NCS S 0502-Y	10,8 м²
О17	плинтус	плинтус МДФ, Orac Decor Contour (Luxxus), h 69 мм, SX165, шелковисто-матовая	NCS S 0300-N	1,3 м
О18	потолок	окраска, Tikkurila, глубокоматовая	NCS S 0300-N	4,7 м²

Примечания

1. Размеры — в мм от чистовых поверхностей стен; условные обозначения и общие указания — лист 2.
2. Двери скрытого монтажа — полотно в плоскости стены, отделка стены по полотну, плинтус прерывается у короба (узел — на листе узлов).

					Проект: Дом 120 м²
	Лист	№ док.	Подпись	Дата	Развёртки стен Б, В. Кладовая (пом. 9)
Дизайнер	Кырлан А.С.			19.10.26	

Стадия	Лист	Листов
П	96	128

выпуск 19.10.2026 № 66b2a77b4d · стр. 96 из 128

Развёртка стены Г


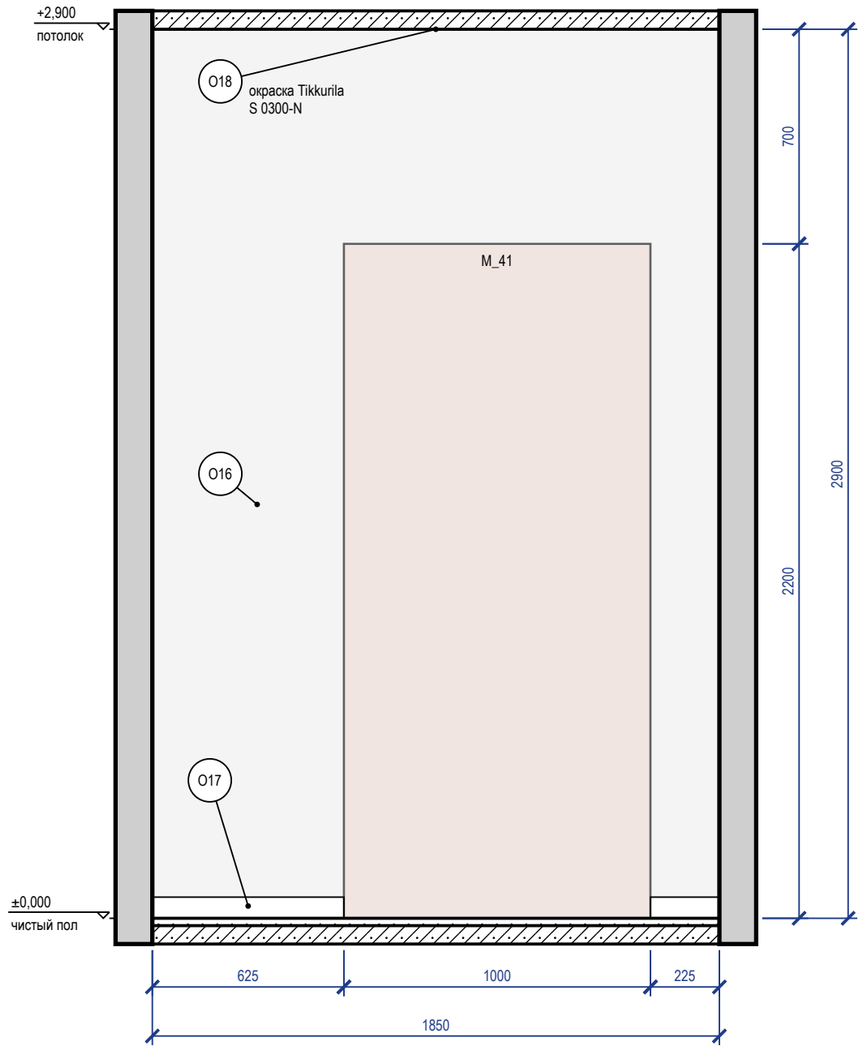


Схема развёрток (М 1:100)

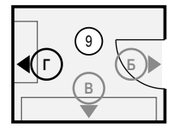

Ведомость отделки (на листе)

Марка	Поверхность	Материал, изделие	Цвет, код	Кол.
О16	стены	окраска, Tikkurila, матовая, подготовка Q3	NCS S 0502-Y	5,4 м²
О17	плинтус	плинтус МДФ, Orac Decor Contour (Luxxus), h 69 мм, SX165, шелковисто-матовая	NCS S 0300-N	0,8 м
О18	потолок	окраска, Tikkurila, глубокоматовая	NCS S 0300-N	4,7 м²

Визуализация этой стены — лист 95



Примечания

1. Размеры — в мм от чистовых поверхностей стен; условные обозначения и общие указания — лист 2.

					Проект: Дом 120 м²	
	Лист	№ док.	Подпись	Дата	Развёртка стены Г. Кладовая (пом. 9)	Стадия / Лист / Листов
Дизайнер	Кырлан А.С.			19.10.26		П / 97 / 128

выпуск 19.10.2026 № 66b2a77b4d · стр. 97 из 128



					Проект: Дом 120 м²
	Лист	№ док.	Подпись	Дата	Визуализация: Холл второго этажа
Дизайнер	Кырлан А.С.			19.10.26	

Стадия	Лист	Листов
П	98	128

выпуск 19.10.2026 № 66b2a77b4d · стр. 98 из 128

Развёртка стены А


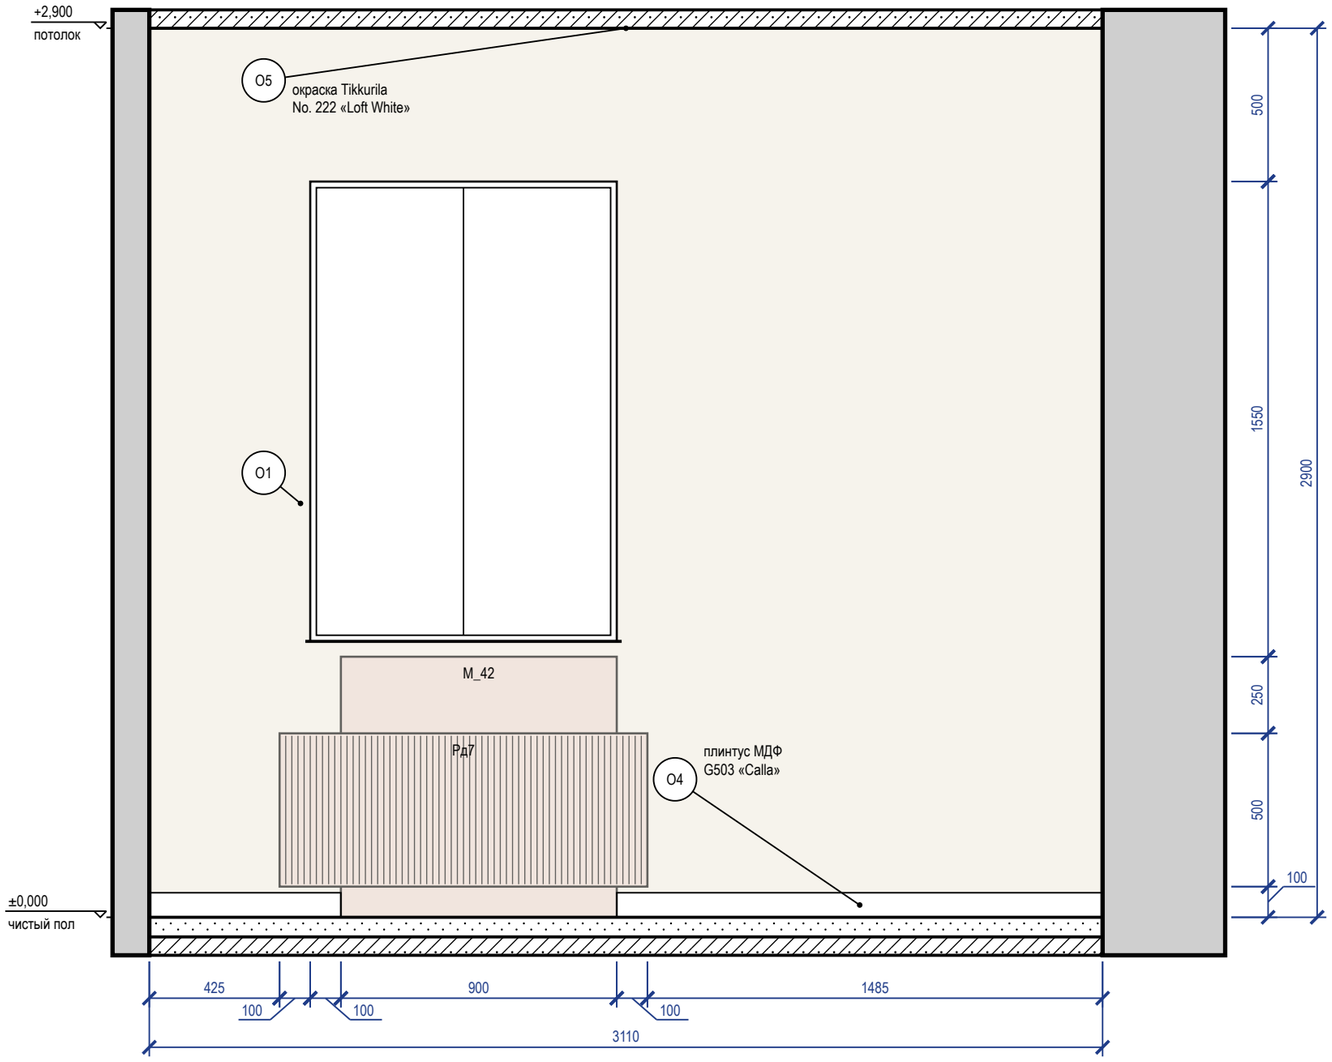


Схема развёрток (М 1:100)

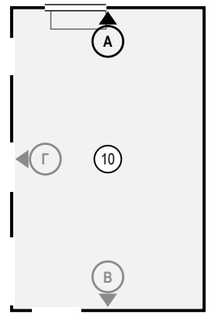

Ведомость отделки (на листе)

Марка	Поверхность	Материал, изделие	Цвет, код	Кол.
О1	стены	окраска, Farrow & Ball Modern Emulsion, матовая, подготовка Q3	Tikkurila G503 «Calla»	7,5 м²
О4	плинтус	плинтус МДФ, h 80 мм, аналог: плинтус МДФ под покраску 80×16	Tikkurila G503 «Calla»	2,2 м
О5	потолок	окраска, Tikkurila Anti-Reflex 2, глубокоматовая, подготовка Q3	Little Greene No. 222 «Loft White»	15,5 м²

Примечания

1. Размеры — в мм от чистовых поверхностей стен; условные обозначения и общие указания — лист 2.

	Лист	№ док.	Подпись	Дата	Проект: Дом 120 м²
Дизайнер	Кырлан А.С.			19.10.26	Развёртка стены А. Холл второго этажа (пом. 10)

Стадия	Лист	Листов
П	99	128

выпуск 19.10.2026 № 66b2a77b4d · стр. 99 из 128

Развёртка стены В


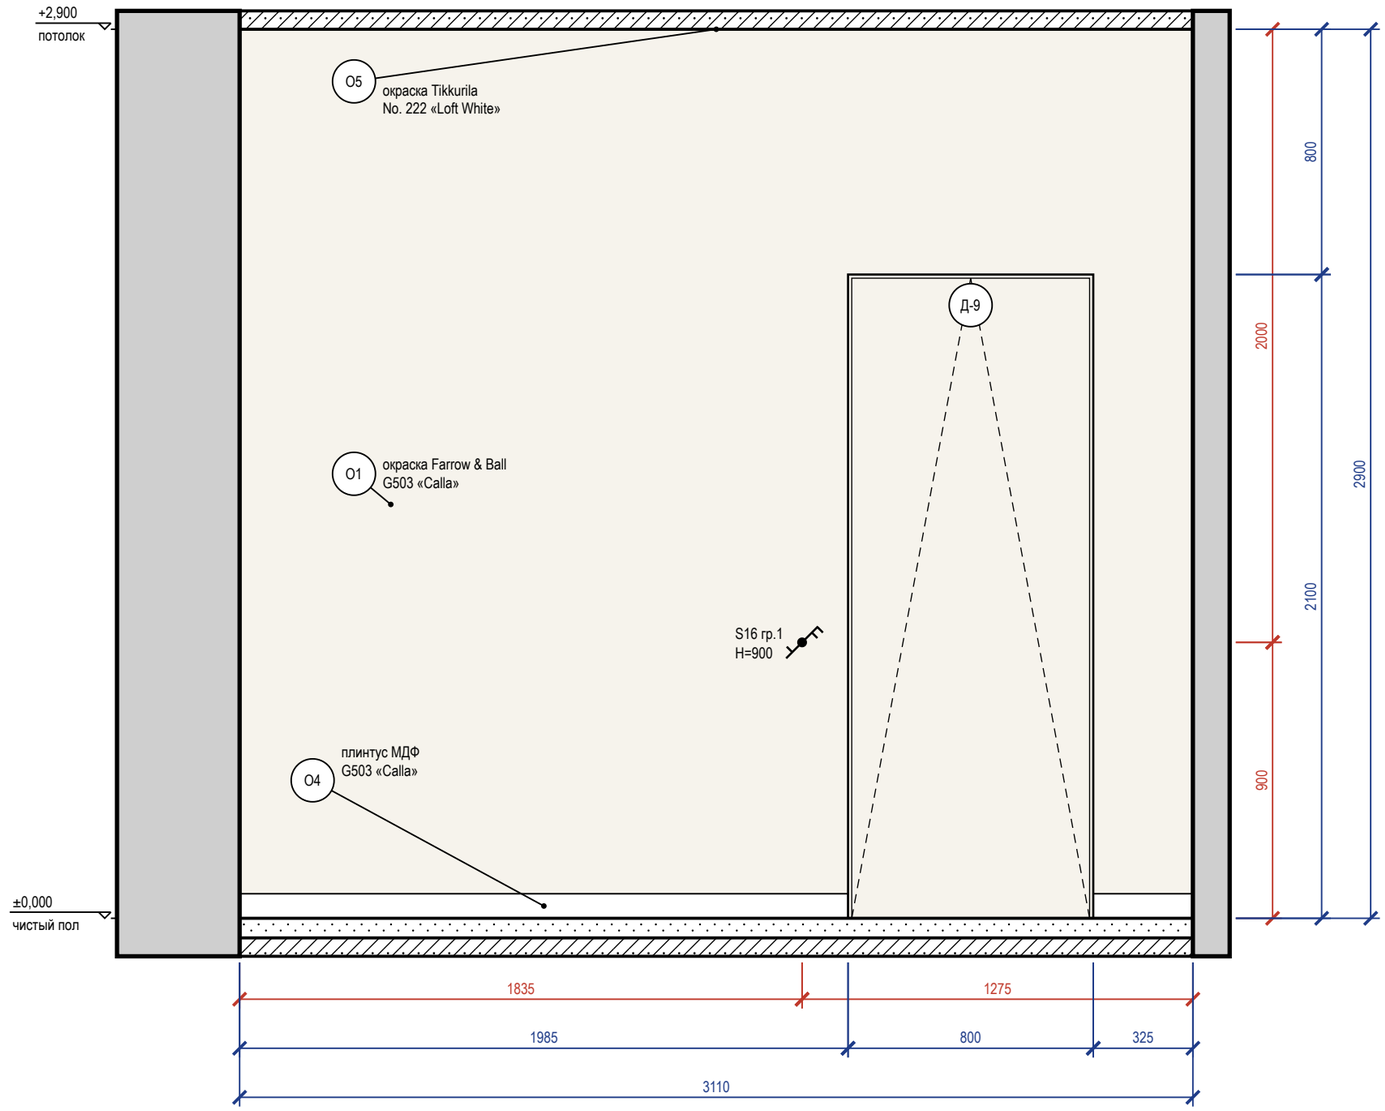


Схема развёрток (М 1:100)

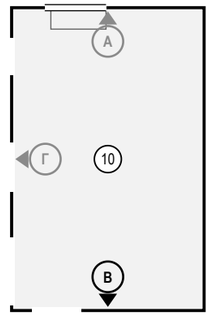

Ведомость отделки (на листе)

Марка	Поверхность	Материал, изделие	Цвет, код	Кол.
О1	стены	окраска, Farrow & Ball Modern Emulsion, матовая, подготовка Q3	Tikkurila G503 «Calla»	7,3 м²
О4	плинтус	плинтус МДФ, h 80 мм, аналог: плинтус МДФ под покраску 80×16	Tikkurila G503 «Calla»	2,3 м
О5	потолок	окраска, Tikkurila Anti-Reflex 2, глубокоматовая, подготовка Q3	Little Greene No. 222 «Loft White»	15,5 м²

Визуализация этой стены — лист 98



Примечания

1. Размеры — в мм от чистовых поверхностей стен; условные обозначения и общие указания — лист 2.
2. Двери скрытого монтажа — полотно в плоскости стены, отделка стены по полотну, плинтус прерывается у короба (узел — на листе узлов).

					Проект: Дом 120 м²
	Лист	№ док.	Подпись	Дата	Развёртка стены В. Холл второго этажа (пом. 10)
Дизайнер	Кырлан А.С.			19.10.26	

Стадия	Лист	Листов
П	100	128

выпуск 19.10.2026 № 66b2a77b4d · стр. 100 из 128

Развёртка стены Г


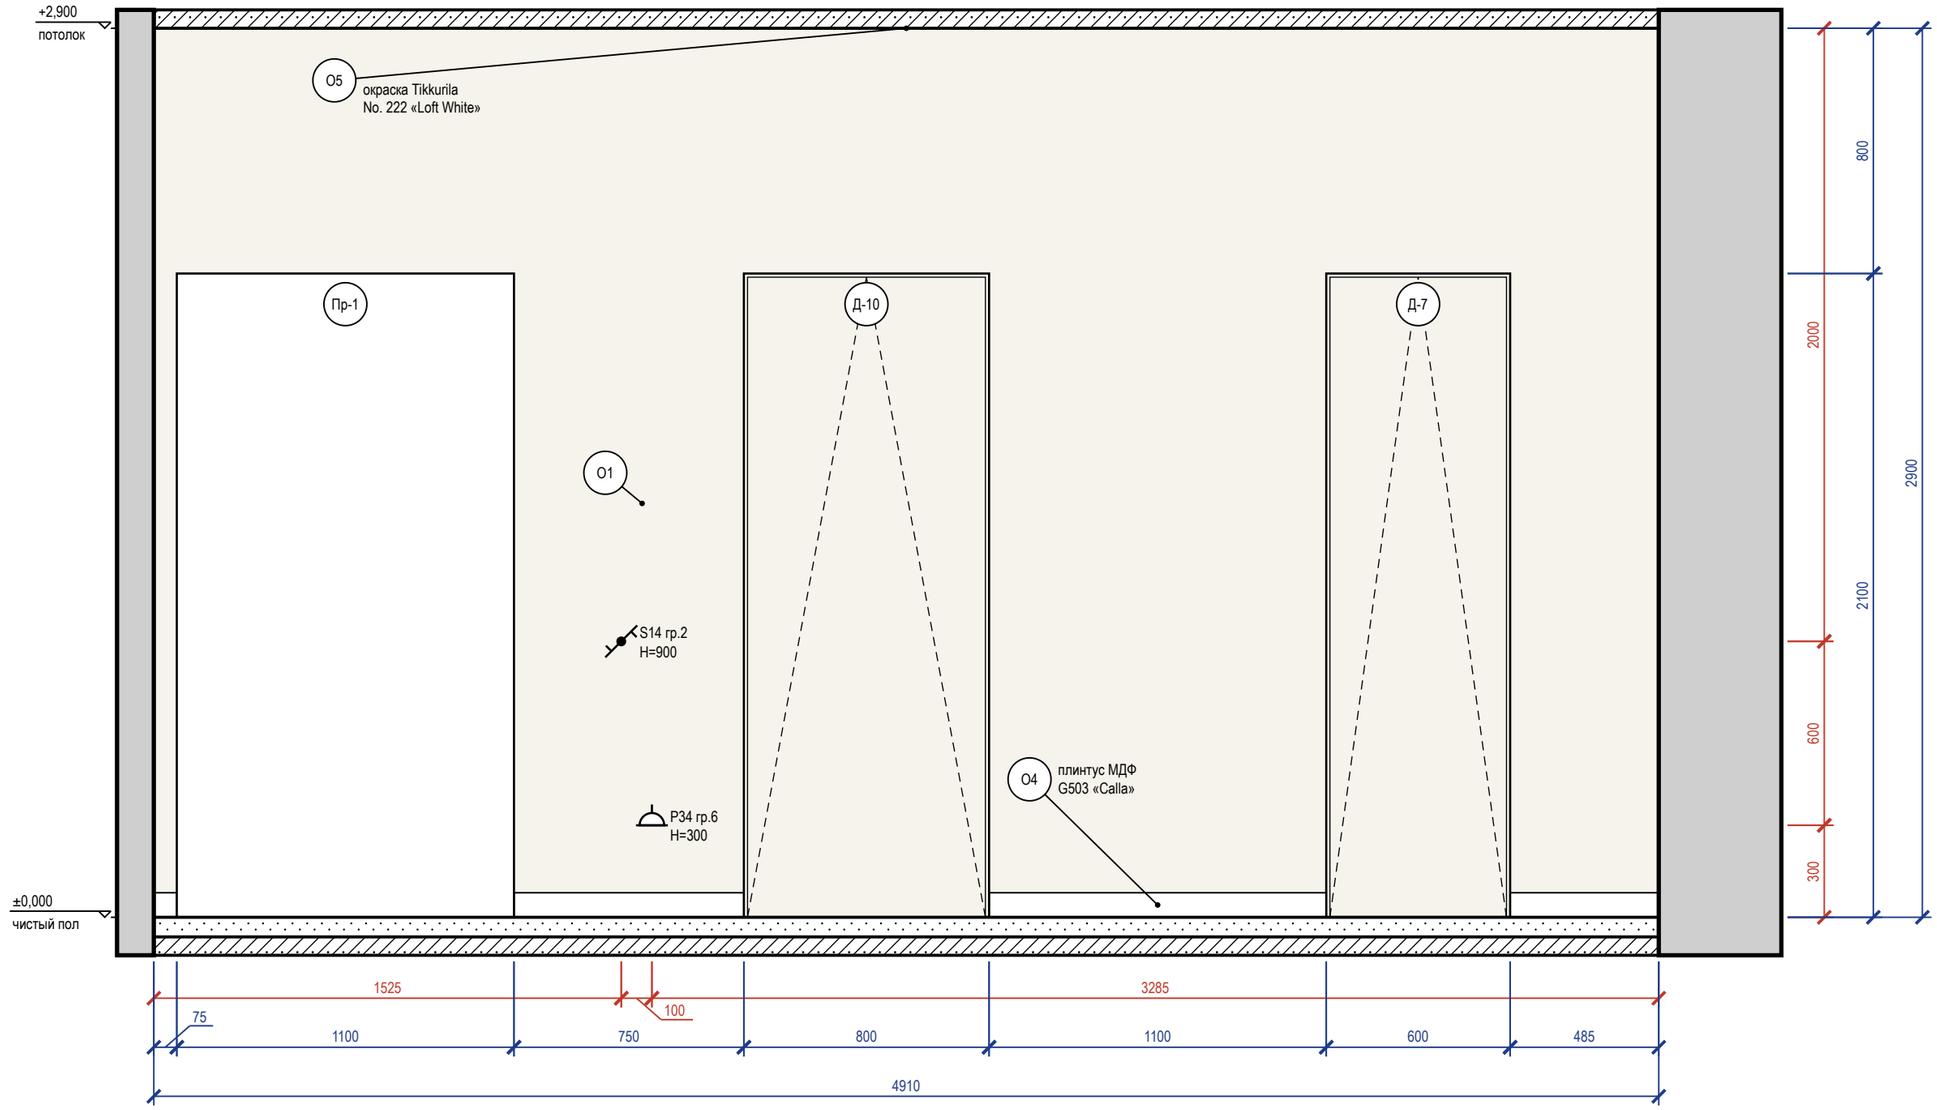


Схема развёрток (М 1:100)

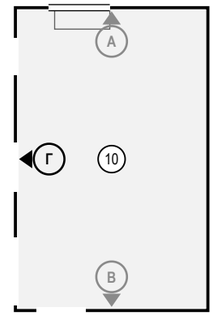

Ведомость отделки (на листе)

Марка	Поверхность	Материал, изделие	Цвет, код	Кол.
О1	стены	окраска, Farrow & Ball Modern Emulsion, матовая, подготовка Q3	Tikkurila G503 «Calla»	9 м²
О4	плинтус	плинтус МДФ, h 80 мм, аналог: плинтус МДФ под покраску 80×16	Tikkurila G503 «Calla»	2,4 м
О5	потолок	окраска, Tikkurila Anti-Reflex 2, глубокоматовая, подготовка Q3	Little Greene No. 222 «Loft White»	15,5 м²

Примечания

1. Размеры — в мм от чистовых поверхностей стен; условные обозначения и общие указания — лист 2.
2. Двери скрытого монтажа — полотно в плоскости стены, отделка стены по полотну, плинтус прерывается у короба (узел — на листе узлов).

	Лист	№ док.	Подпись	Дата	
Дизайнер	Кырлан А.С.			19.10.26	Развёртка стены Г. Холл второго этажа (пом. 10)

Проект: Дом 120 м²

Стадия	Лист	Листов
П	101	128

выпуск 19.10.2026 № 66b2a77b4d · стр. 101 из 128




					Проект: Дом 120 м²
	Лист	№ док.	Подпись	Дата	Визуализация: Коридор второго этажа
Дизайнер	Кырлан А.С.			19.10.26	

Стадия	Лист	Листов
П	102	128

выпуск 19.10.2026 № 66b2a77b4d · стр. 102 из 128

Развёртка стены А

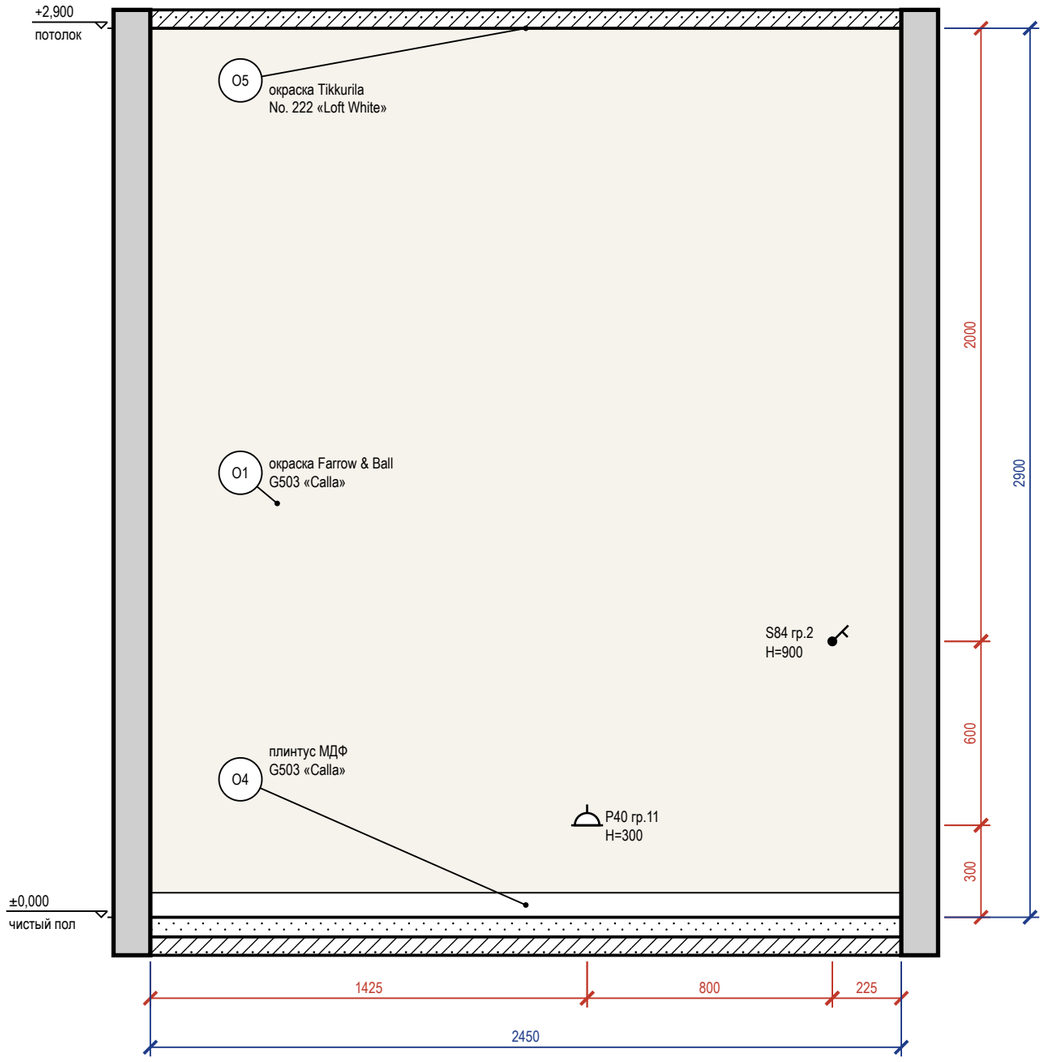

Развёртка стены В


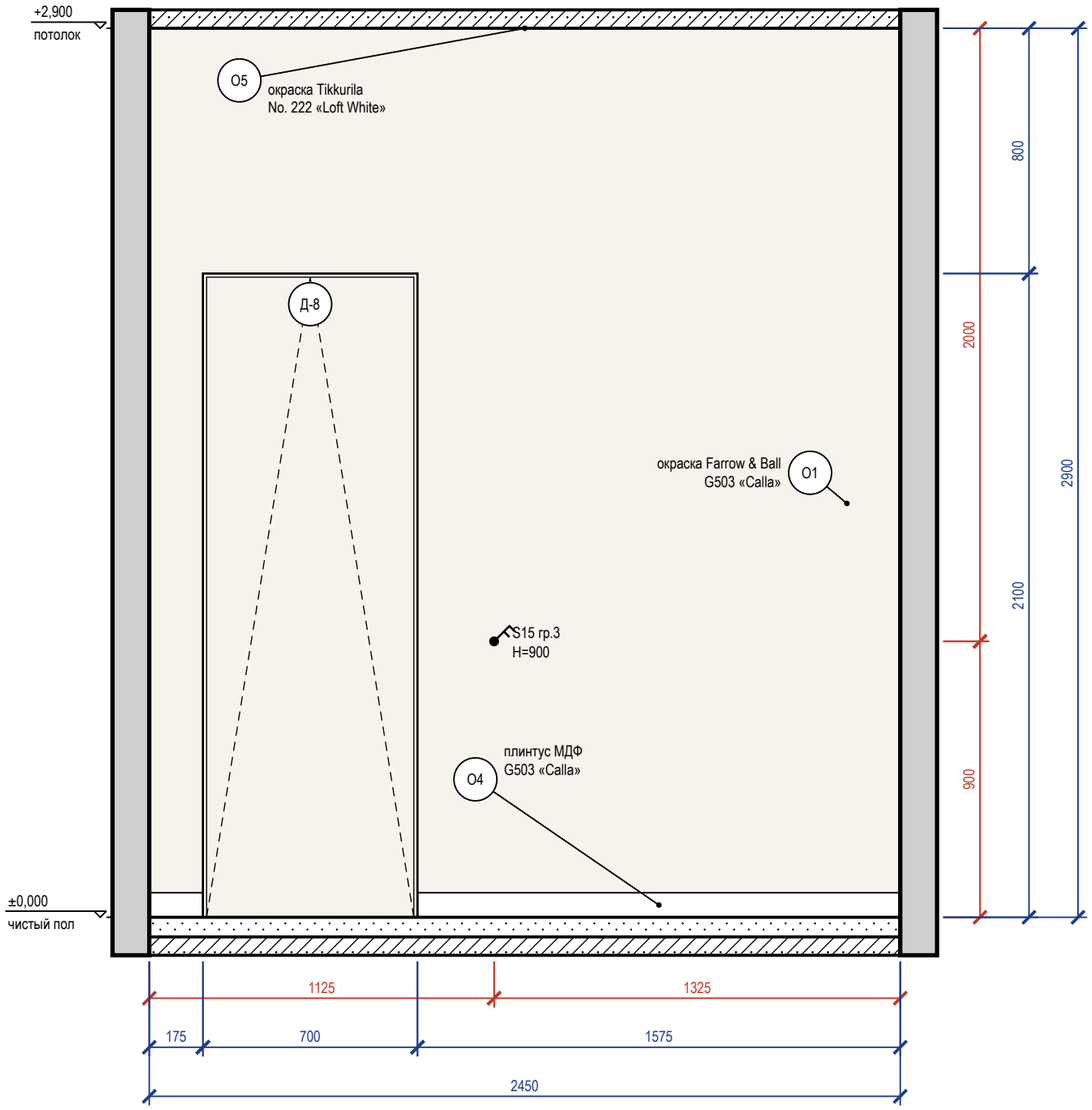


Схема развёрток (М 1:100)

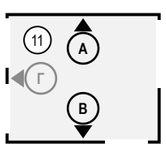

Ведомость отделки (на листе)

Марка	Поверхность	Материал, изделие	Цвет, код	Кол.
О1	стены	окраска, Farrow & Ball Modern Emulsion, матовая, подготовка Q3	Tikkurila G503 «Calla»	12,7 м²
О4	плинтус	плинтус МДФ, h 80 мм, аналог: плинтус МДФ под покраску 80×16	Tikkurila G503 «Calla»	4,2 м
О5	потолок	окраска, Tikkurila Anti-Reflex 2, глубокоматовая, подготовка Q3	Little Greene No. 222 «Loft White»	5,2 м²

Примечания

1. Размеры — в мм от чистовых поверхностей стен; условные обозначения и общие указания — лист 2.
2. Двери скрытого монтажа — полотно в плоскости стены, отделка стены по полотну, плинтус прерывается у короба (узел — на листе узлов).

					Проект: Дом 120 м²
	Лист	№ док.	Подпись	Дата	Развёртки стен А, В. Коридор второго этажа (пом. 11)
Дизайнер	Кырлан А.С.			19.10.26	

Стадия	Лист	Листов
П	103	128

выпуск 19.10.2026 № 66b2a77b4d · стр. 103 из 128

Развёртка стены Г


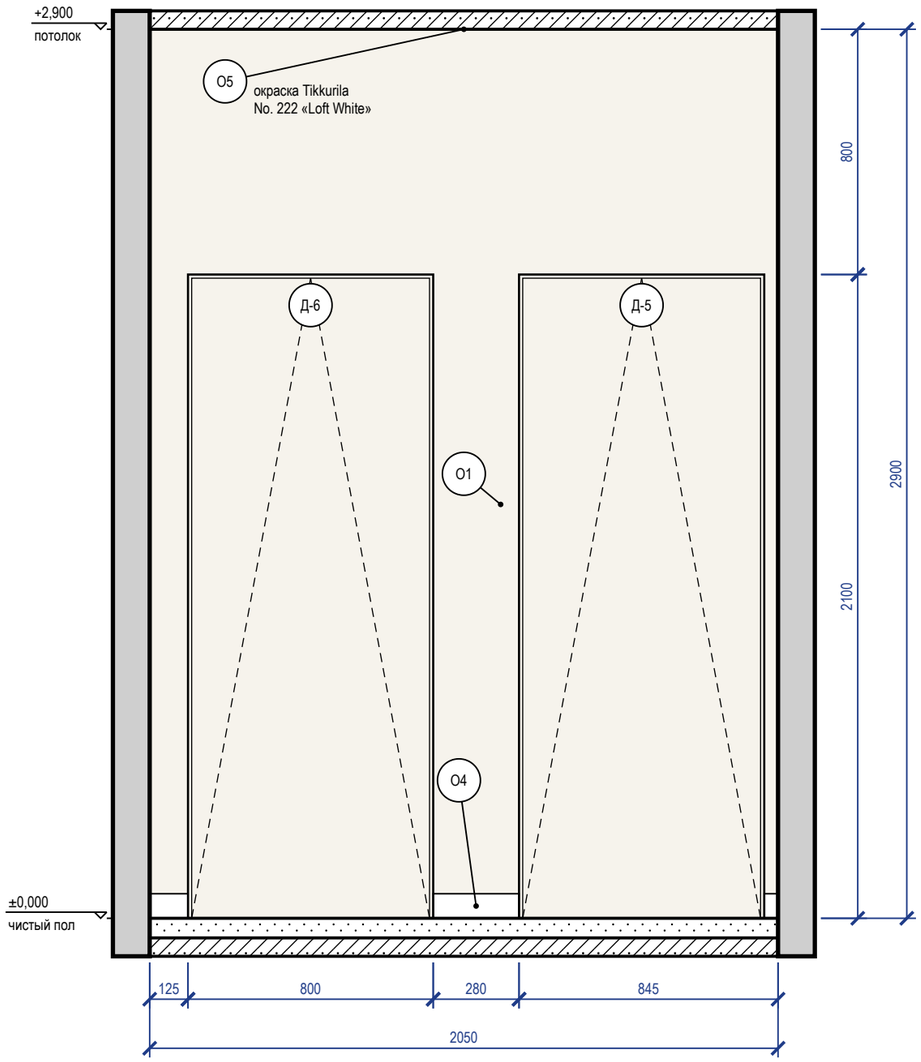


Схема развёрток (М 1:100)

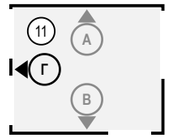

Ведомость отделки (на листе)

Марка	Поверхность	Материал, изделие	Цвет, код	Кол.
О1	стены	окраска, Farrow & Ball Modern Emulsion, матовая, подготовка Q3	Tikkurila G503 «Calla»	2,6 м²
О4	плинтус	плинтус МДФ, h 80 мм, аналог: плинтус МДФ под покраску 80×16	Tikkurila G503 «Calla»	0,5 м
О5	потолок	окраска, Tikkurila Anti-Reflex 2, глубокоматовая, подготовка Q3	Little Greene No. 222 «Loft White»	5,2 м²

Визуализация этой стены — лист 102



Примечания

1. Размеры — в мм от чистовых поверхностей стен; условные обозначения и общие указания — лист 2.
2. Двери скрытого монтажа — полотно в плоскости стены, отделка стены по полотну, плинтус прерывается у короба (узел — на листе узлов).

					Проект: Дом 120 м²
	Лист	№ док.	Подпись	Дата	Развёртка стены Г. Коридор второго этажа (пом. 11)
Дизайнер	Кырлан А.С.			19.10.26	

Стадия	Лист	Листов
П	104	128

выпуск 19.10.2026 № 66b2a77b4d · стр. 104 из 128



					Проект: Дом 120 м²
	Лист	№ док.	Подпись	Дата	
Дизайнер	Кырлан А.С.			19.10.26	Визуализация: Детская вторая

Стадия	Лист	Листов
П	105	128

выпуск 19.10.2026 № 66b2a77b4d · стр. 105 из 128



					Проект: Дом 120 м²
	Лист	№ док.	Подпись	Дата	
Дизайнер	Кырлан А.С.			19.10.26	Визуализация: Детская вторая

Стадия	Лист	Листов
П	106	128

выпуск 19.10.2026 № 66b2a77b4d · стр. 106 из 128

Развёртка стены А


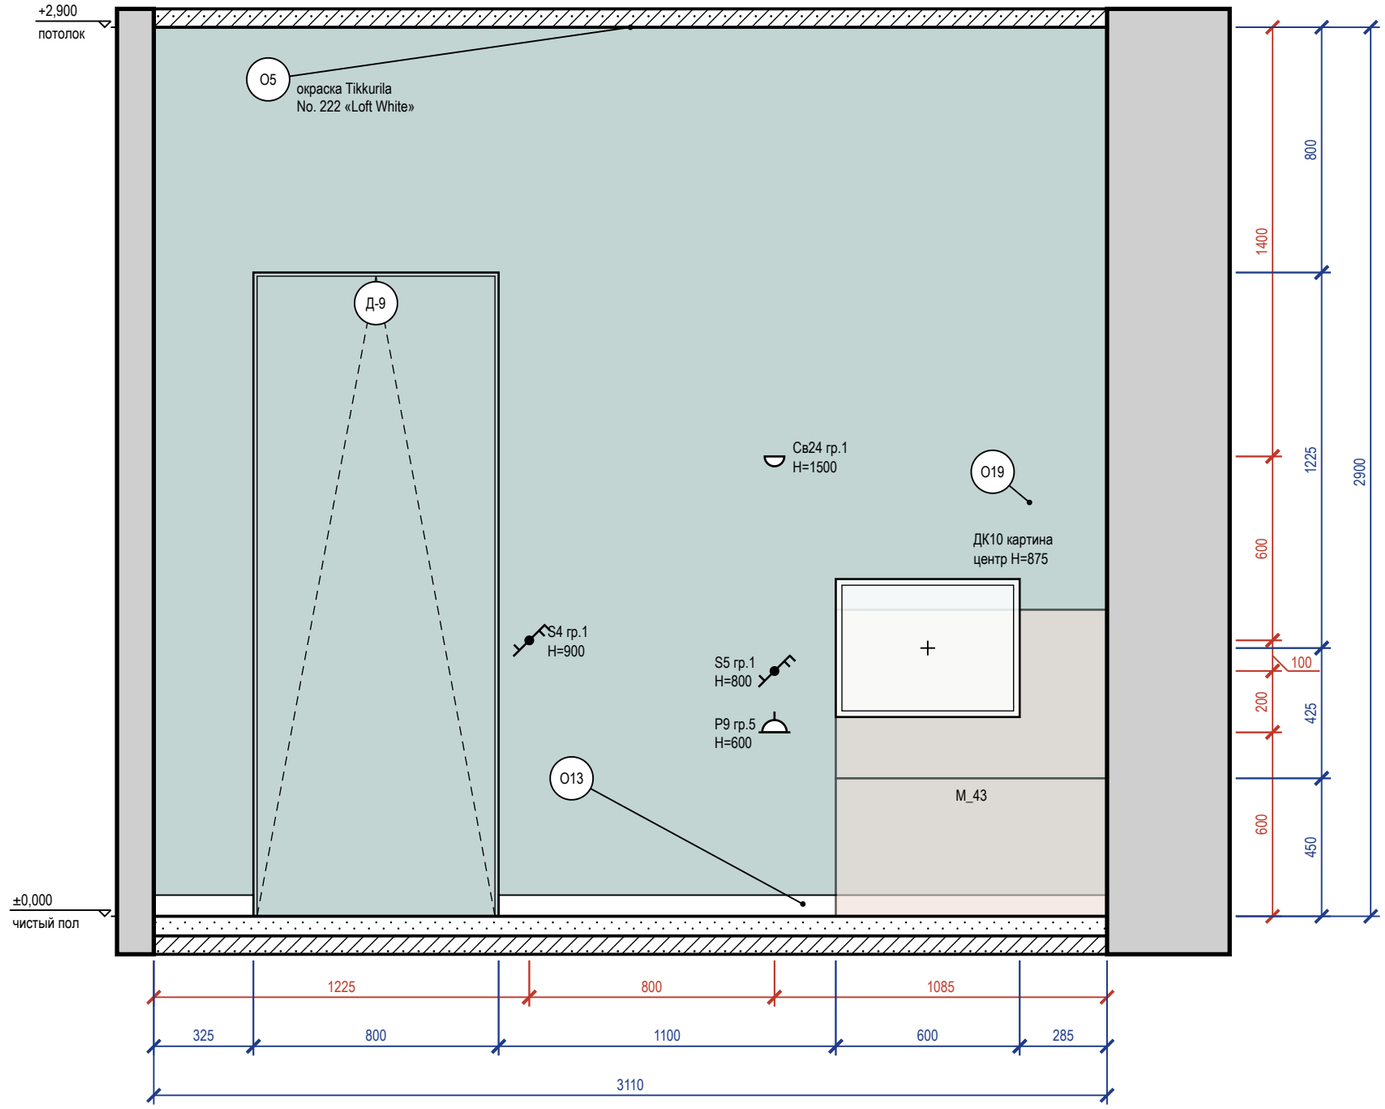


Схема развёрток (М 1:100)

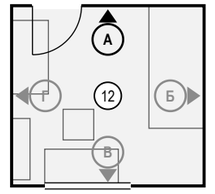

Ведомость отделки (на листе)

Марка	Поверхность	Материал, изделие	Цвет, код	Кол.
О5	потолок	окраска, Tikkurila Anti-Reflex 2, глубокоматовая, подготовка Q3	Little Greene No. 222 «Loft White»	9,2 м²
О13	плинтус	плинтус МДФ, Orac Decor Contour (Luxxus), h 69 мм, SX165	Tikkurila G503 «Calla»	2,3 м
О19	акцентная стена	окраска, Farrow & Ball Modern Emulsion, матовая, подготовка Q3	Tikkurila H440 «H440 Wave бирюзово-голубая вода»	7,3 м²

Визуализация этой стены



Примечания

1. Размеры — в мм от чистовых поверхностей стен; условные обозначения и общие указания — лист 2.
2. Картины и зеркала крепить к основанию по паспорту изделия (закладные и анкеры — в перечне скрытых работ); крест — ось центра предмета.
3. Двери скрытого монтажа — полотно в плоскости стены, отделка стены по полотну, плинтус прерывается у короба (узел — на листе узлов).

					Проект: Дом 120 м²
	Лист	№ док.	Подпись	Дата	Развёртка стены А. Детская вторая (пом. 12)
Дизайнер	Кырлан А.С.			19.10.26	

Стадия	Лист	Листов
П	107	128

выпуск 19.10.2026 № 66b2a77b4d · стр. 107 из 128

Развёртка стены Б


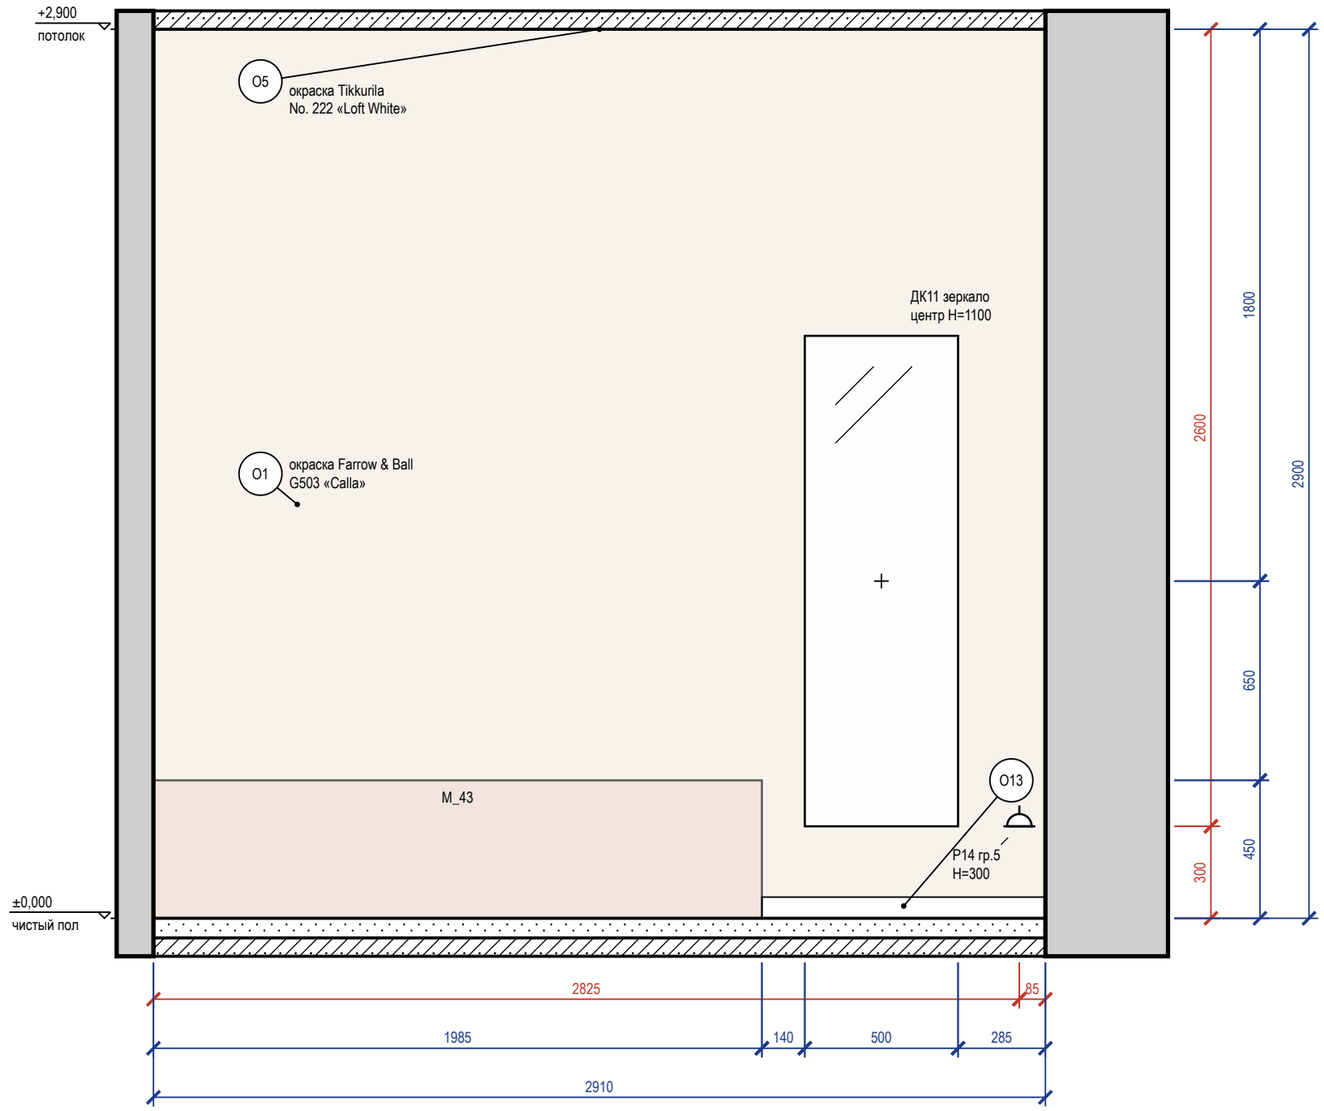



Схема развёрток (М 1:100)

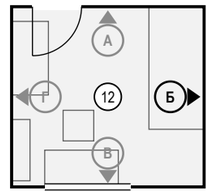

Ведомость отделки (на листе)

Марка	Поверхность	Материал, изделие	Цвет, код	Кол.
О1	стены	окраска, Farrow & Ball Modern Emulsion, матовая, подготовка Q3	Tikkurila G503 «Calla»	8,4 м²
О5	потолок	окраска, Tikkurila Anti-Reflex 2, глубокоматовая, подготовка Q3	Little Greene No. 222 «Loft White»	9,2 м²
О13	плинтус	плинтус МДФ, Orac Decor Contour (Luxxus), h 69 мм, SX165	Tikkurila G503 «Calla»	0,9 м

Визуализация этой стены

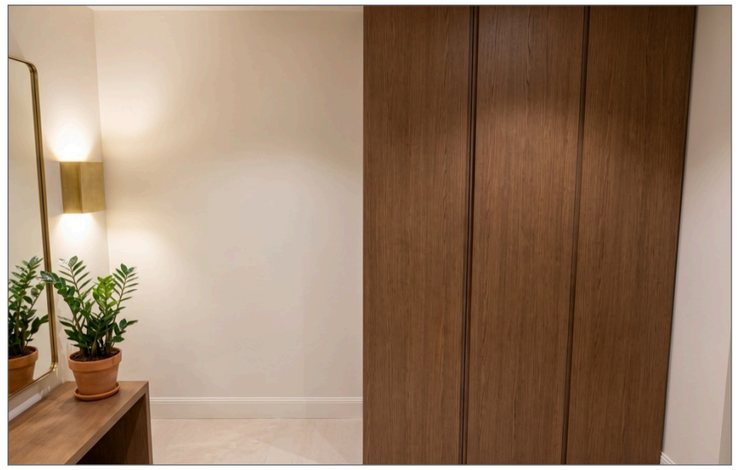

Примечания

1. Размеры — в мм от чистовых поверхностей стен; условные обозначения и общие указания — лист 2.
2. Картины и зеркала крепить к основанию по паспорту изделия (закладные и анкеры — в перечне скрытых работ); крест — ось центра предмета.

					Проект: Дом 120 м²
	Лист	№ док.	Подпись	Дата	Развёртка стены Б. Детская вторая (пом. 12)
Дизайнер	Кырлан А.С.			19.10.26	

Стадия	Лист	Листов
П	108	128

выпуск 19.10.2026 № 66b2a77b4d · стр. 108 из 128

Развёртка стены В


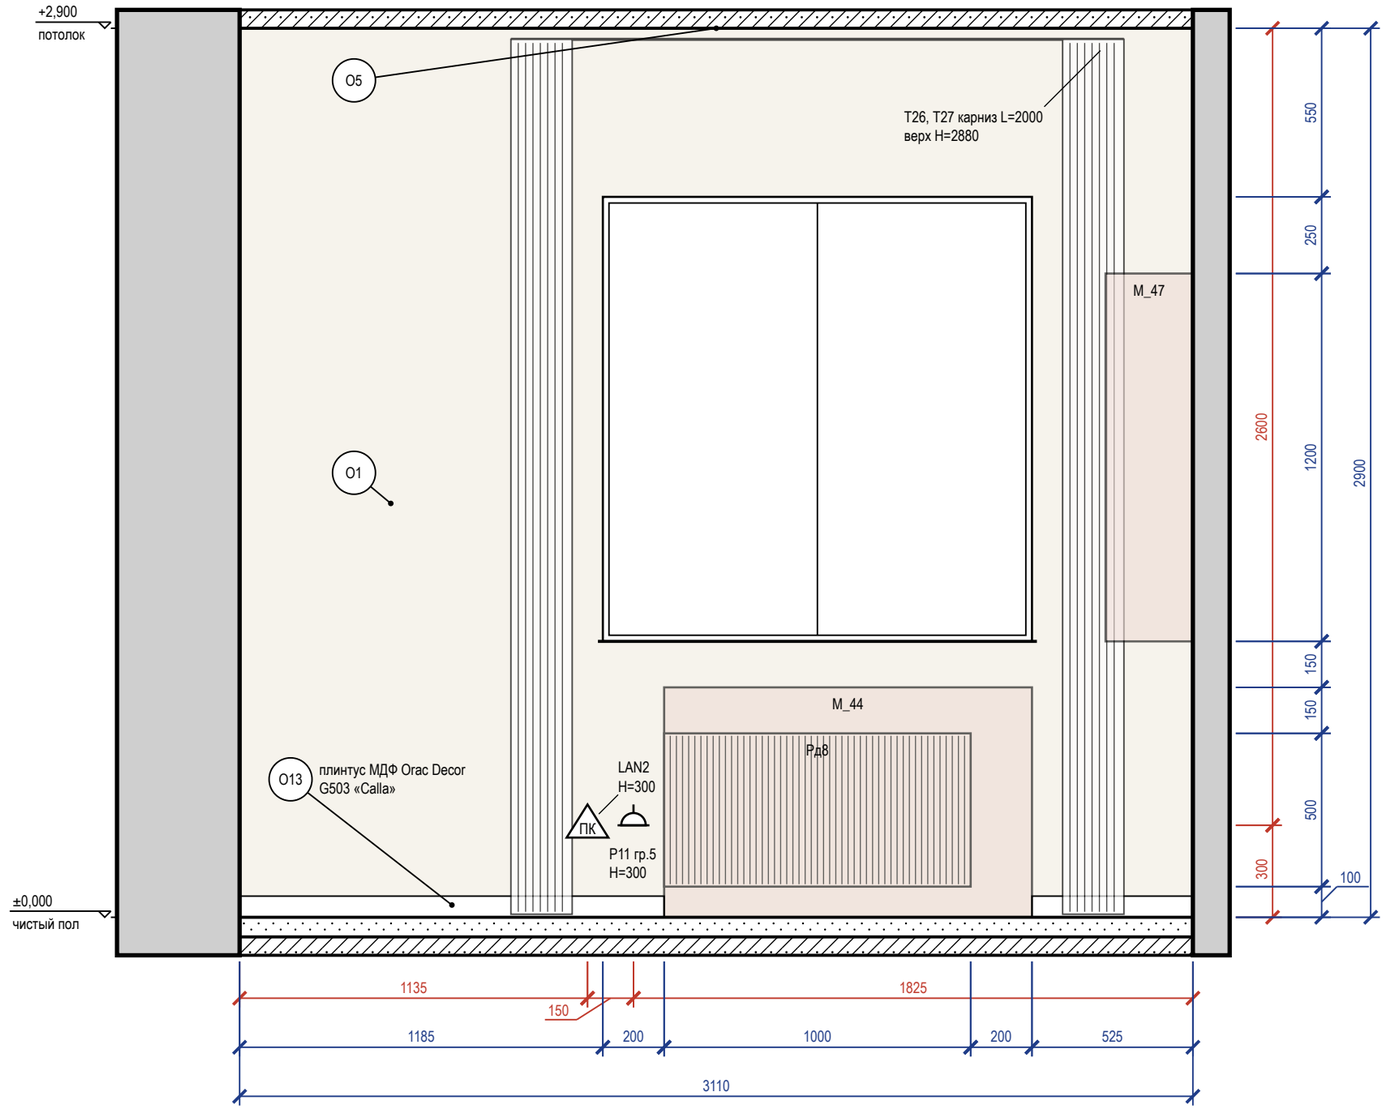


Схема развёрток (М 1:100)

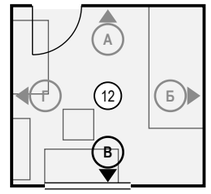

Ведомость отделки (на листе)

Марка	Поверхность	Материал, изделие	Цвет, код	Кол.
О1	стены	окраска, Farrow & Ball Modern Emulsion, матовая, подготовка Q3	Tikkurila G503 «Calla»	7 м²
О5	потолок	окраска, Tikkurila Anti-Reflex 2, глубокоматовая, подготовка Q3	Little Greene No. 222 «Loft White»	9,2 м²
О13	плинтус	плинтус МДФ, Orac Decor Contour (Luxxus), h 69 мм, SX165	Tikkurila G503 «Calla»	1,9 м

Примечания

1. Размеры — в мм от чистовых поверхностей стен; условные обозначения и общие указания — лист 2.
2. Карнизы (шины) — по ведомости текстиля декоратора; длина L и верх H — по развёртке, крепление — до окраски потолка.

	Лист	№ док.	Подпись	Дата	Проект: Дом 120 м²
Дизайнер	Кырлан А.С.			19.10.26	Развёртка стены В. Детская вторая (пом. 12)

Стадия	Лист	Листов
П	109	128

выпуск 19.10.2026 № 66b2a77b4d · стр. 109 из 128

Развёртка стены Г


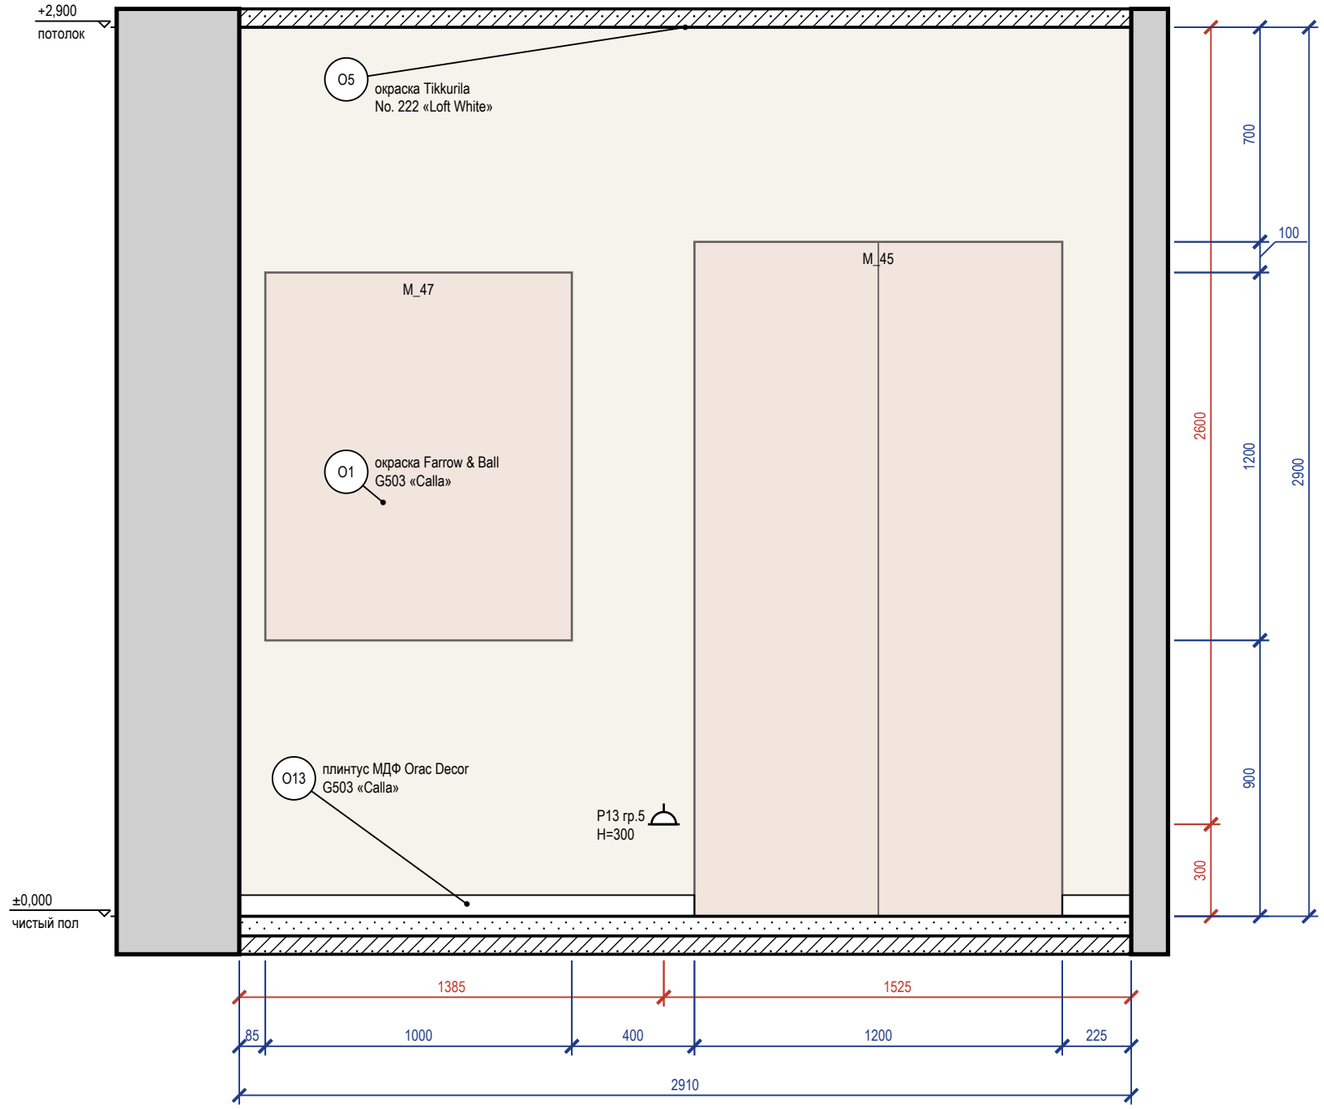


Схема развёрток (М 1:100)

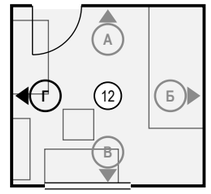

Ведомость отделки (на листе)

Марка	Поверхность	Материал, изделие	Цвет, код	Кол.
О1	стены	окраска, Farrow & Ball Modern Emulsion, матовая, подготовка Q3	Tikkurila G503 «Calla»	8,4 м²
О5	потолок	окраска, Tikkurila Anti-Reflex 2, глубокоматовая, подготовка Q3	Little Greene No. 222 «Loft White»	9,2 м²
О13	плинтус	плинтус МДФ, Orac Decor Contour (Luxxus), h 69 мм, SX165	Tikkurila G503 «Calla»	1,7 м

Визуализация этой стены — лист 106



Примечания

1. Размеры — в мм от чистовых поверхностей стен; условные обозначения и общие указания — лист 2.

					Проект: Дом 120 м²
	Лист	№ док.	Подпись	Дата	Развёртка стены Г. Детская вторая (пом. 12)
Дизайнер	Кырлан А.С.			19.10.26	

Стадия	Лист	Листов
П	110	128

выпуск 19.10.2026 № 66b2a77b4d · стр. 110 из 128




					Проект: Дом 120 м²
	Лист	№ док.	Подпись	Дата	Визуализация: Санузел второго этажа
Дизайнер	Кырлан А.С.			19.10.26	

Стадия	Лист	Листов
П	111	128

выпуск 19.10.2026 № 66b2a77b4d · стр. 111 из 128

Развёртка стены А

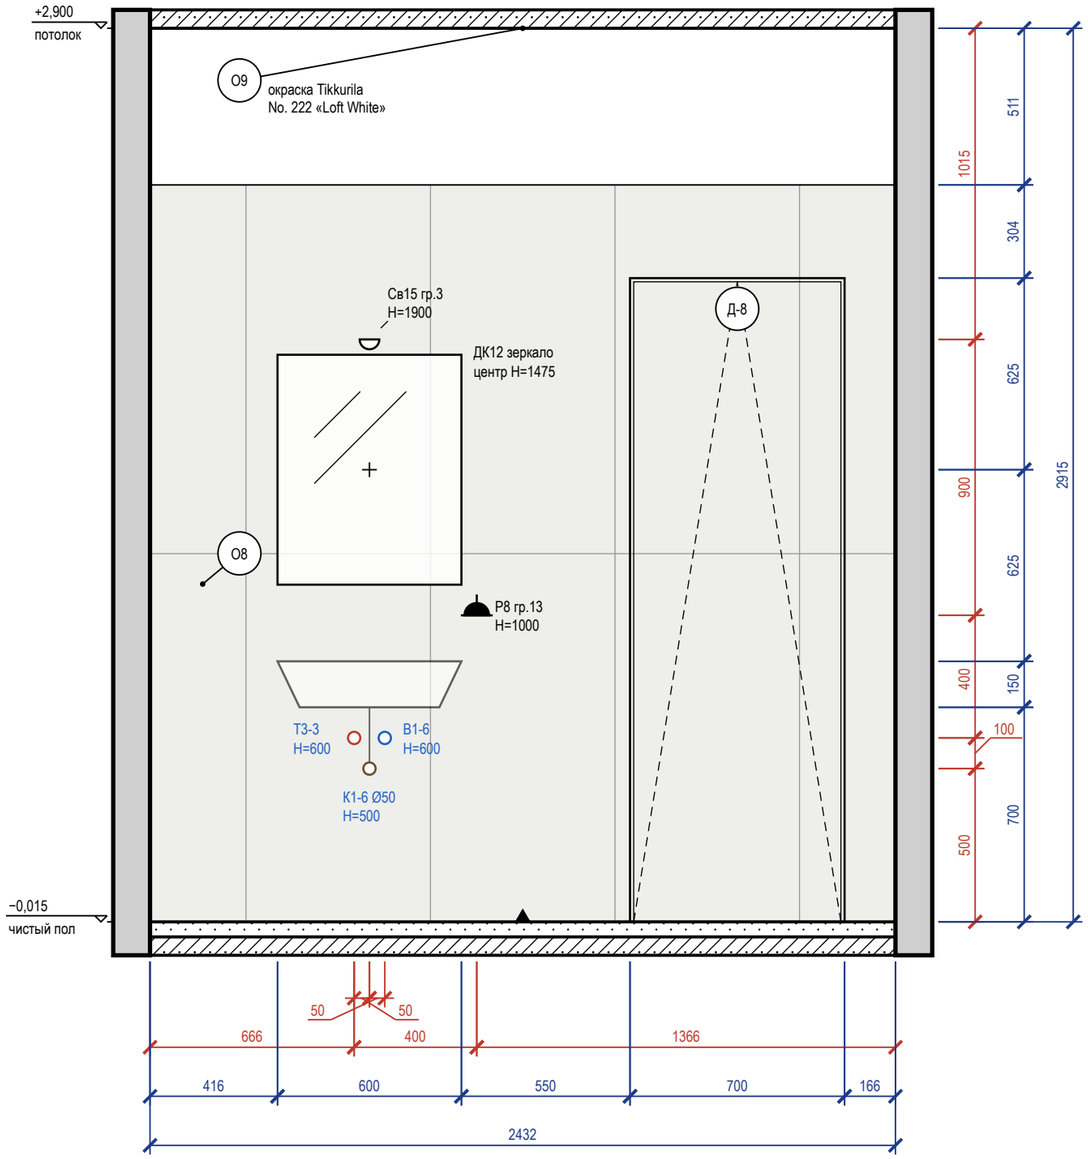

Развёртка стены Б


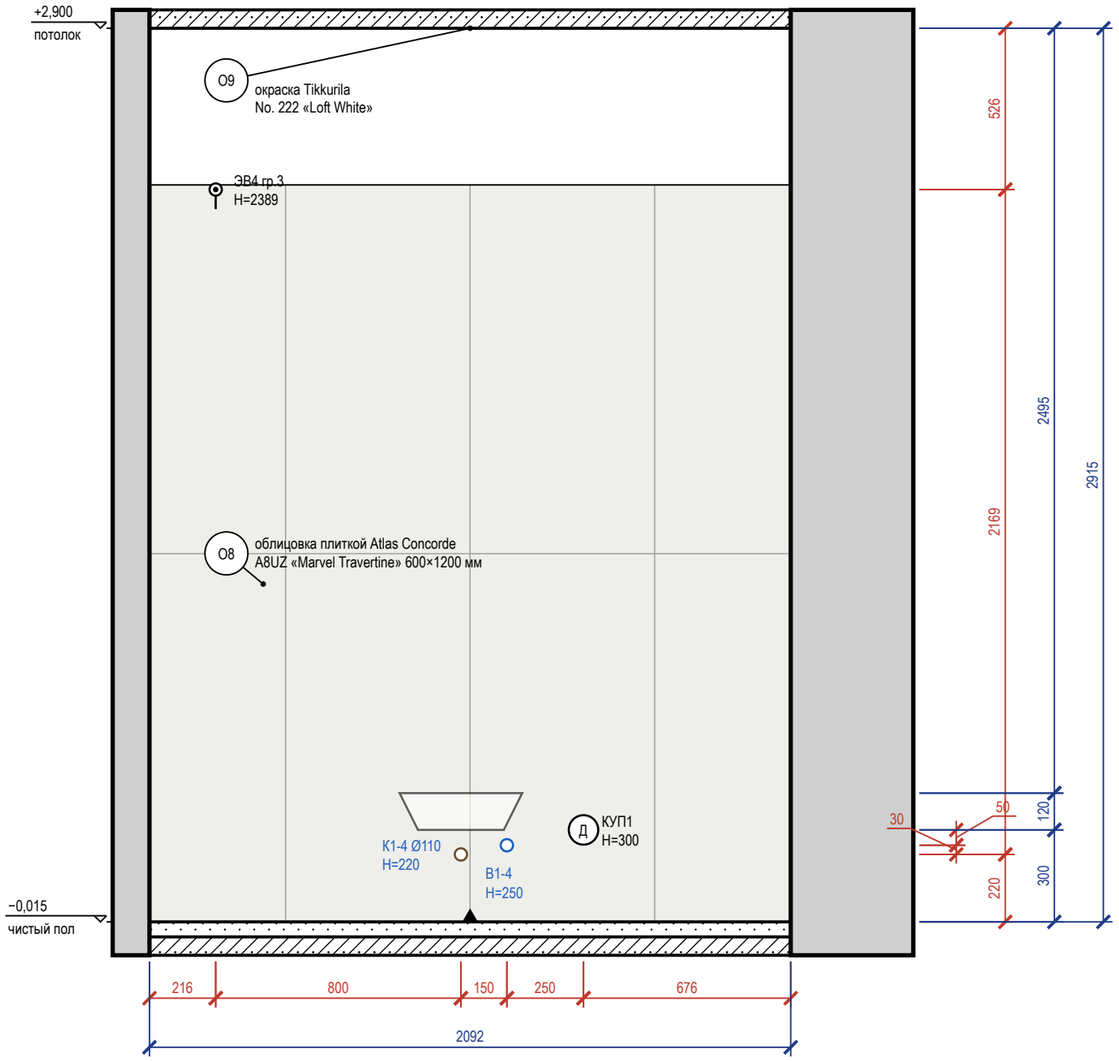


Схема развёрток (М 1:100)

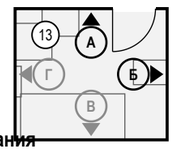

Ведомость отделки (на листе)

Марка	Поверхность	Материал, изделие	Цвет, код	Кол.
О8	стены	облицовка плиткой, Atlas Concorde Marvel Travertine, 600×1200×9 мм, A8UZ, затирка CG2WA	Atlas Concorde A8UZ «Marvel Travertine»	9,4 м²
О9	потолок	окраска, Tikkurila Luja 7, матовая, подготовка Q3	Little Greene No. 222 «Loft White»	5,3 м²

Примечания

1. Размеры — в мм от чистовых поверхностей стен; условные обозначения и общие указания — лист 2.
2. Схема мебели, приборов и декора не является технической документацией для производства мебели; габариты — по паспортам изделий.
3. Выводы ВК — коды и высоты по листу выводов сантехники.
4. Облицовка — по сетке швов 2 мм, раскладка от оси стены (треугольник у пола), целые ряды от пола; подрезки — по листу раскладки плитки.
5. Гидроизоляция в 2 слоя, заход на стены 200 мм — до облицовки, с актом скрытых работ и тестом проливом (узел — на листе узлов).
6. Картины и зеркала крепить к основанию по паспорту изделия (закладные и анкеры — в перечне скрытых работ); крест — ось центра предмета.
7. Двери скрытого монтажа — полотно в плоскости стены, отделка стены по полотну, плинтус прерывается у короба (узел — на листе узлов).

					Проект: Дом 120 м²
	Лист	№ док.	Подпись	Дата	Развёртки стен А, Б. Санузел второго этажа (пом. 13)
Дизайнер	Кырлан А.С.			19.10.26	

Стадия	Лист	Листов
П	112	128

выпуск 19.10.2026 № 66b2a77b4d · стр. 112 из 128

Развёртка стены В


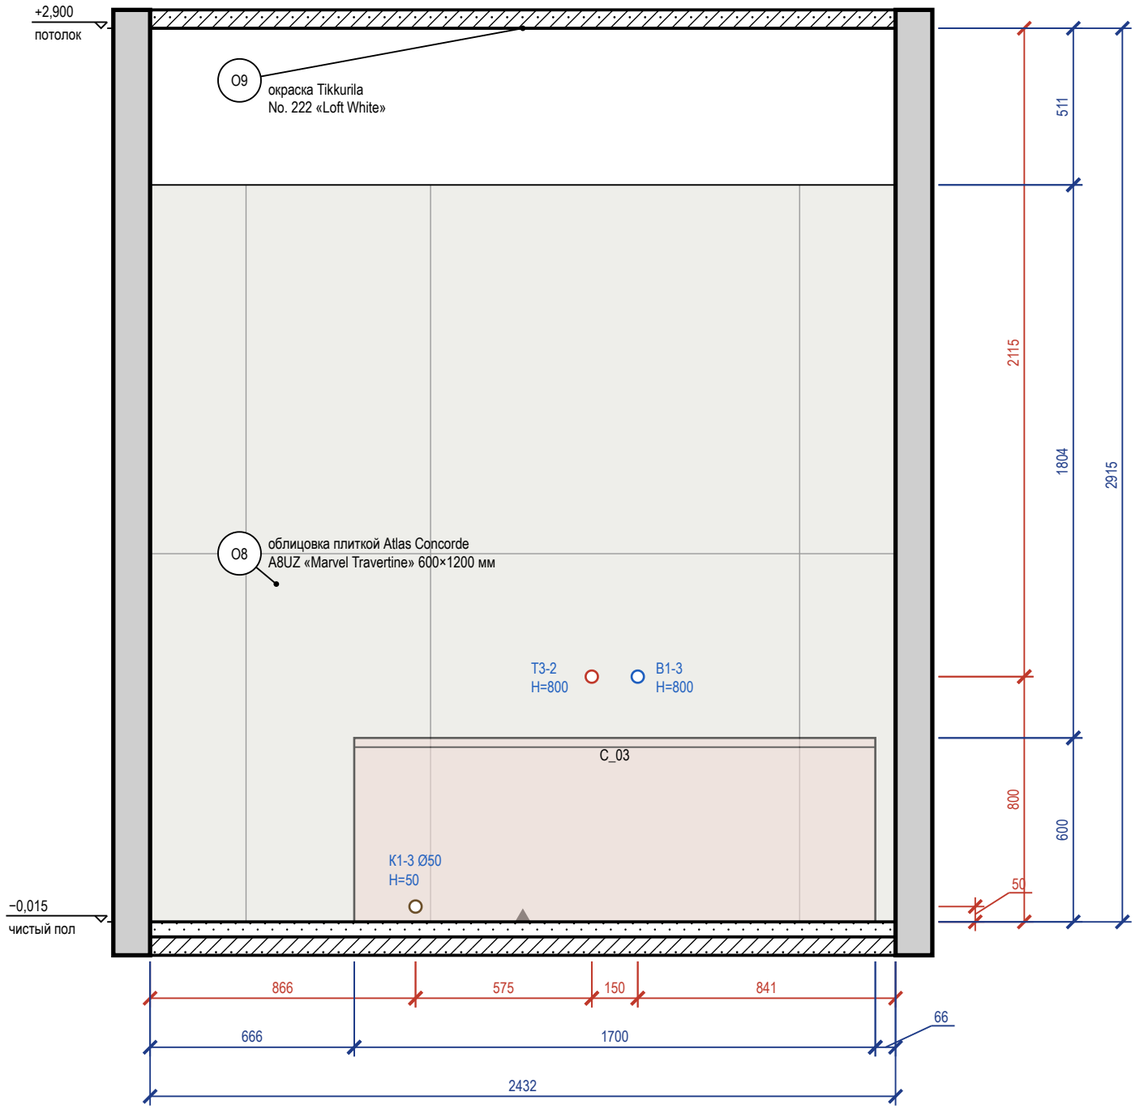


Схема развёрток (М 1:100)

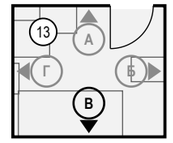

Ведомость отделки (на листе)

Марка	Поверхность	Материал, изделие	Цвет, код	Кол.
O8	стены	облицовка плиткой, Atlas Concorde Marvel Travertine, 600×1200×9 мм, A8UZ, затирка CG2WA	Atlas Concorde A8UZ «Marvel Travertine»	5,8 м²
O9	потолок	окраска, Tikkurila Luja 7, матовая, подготовка Q3	Little Greene No. 222 «Loft White»	5,3 м²

Примечания

1. Размеры — в мм от чистовых поверхностей стен; условные обозначения и общие указания — лист 2.
2. Схема мебели, приборов и декора не является технической документацией для производства мебели; габариты — по паспортам изделий.
3. Выводы ВК — коды и высоты по листу выводов сантехники.
4. Облицовка — по сетке швов 2 мм, раскладка от оси стены (треугольник у пола), целые ряды от пола; подрезки — по листу раскладки плитки.
5. Гидроизоляция в 2 слоя, заход на стены 200 мм — до облицовки, с актом скрытых работ и тестом проливом (узел — на листе узлов).

					Проект: Дом 120 м²
	Лист	№ док.	Подпись	Дата	Развёртка стены В. Санузел второго этажа (пом. 13)
Дизайнер	Кырлан А.С.			19.10.26	

Стадия	Лист	Листов
П	113	128

выпуск 19.10.2026 № 66b2a77b4d · стр. 113 из 128

Развёртка стены Г


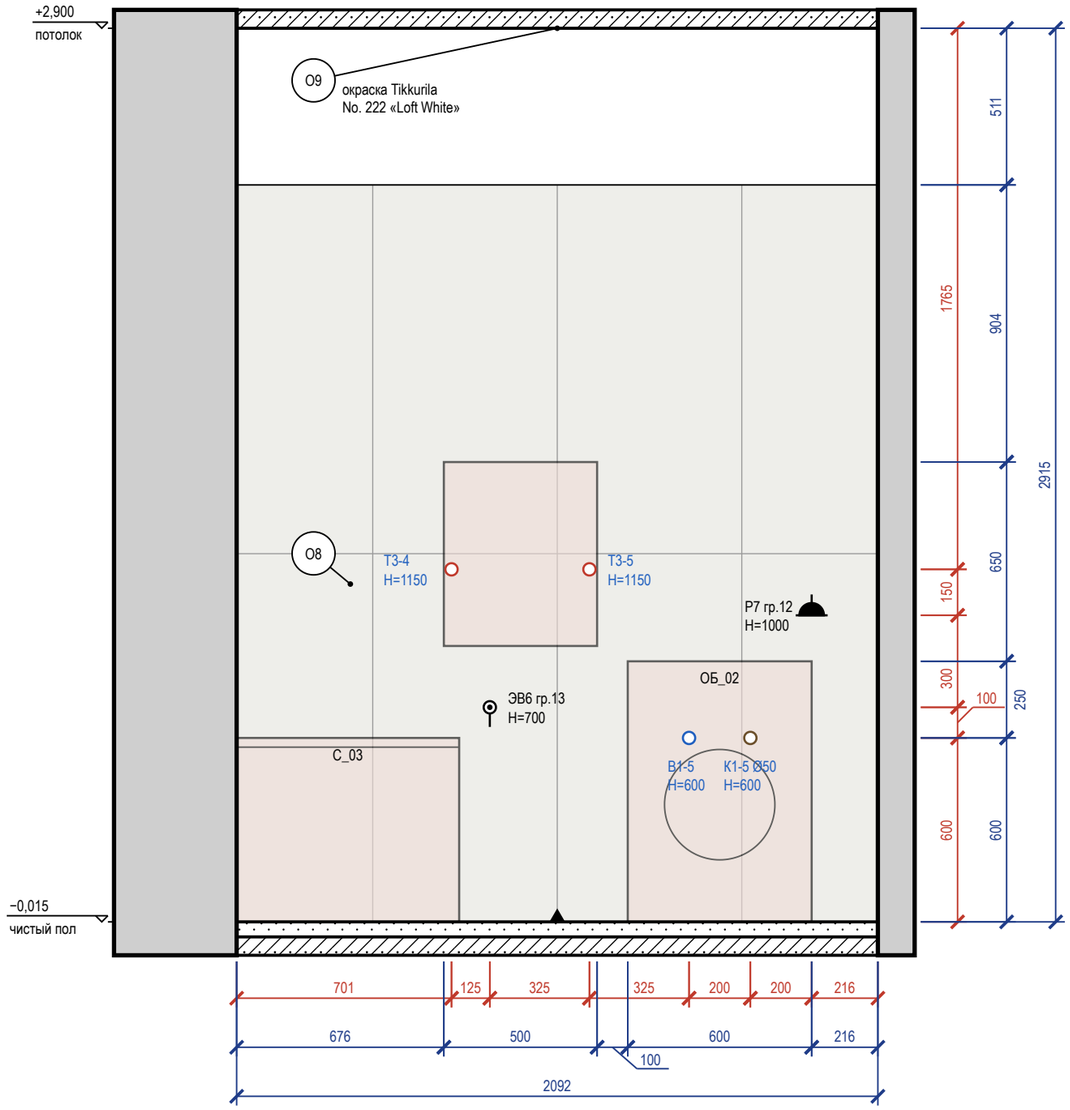


Схема развёрток (М 1:100)

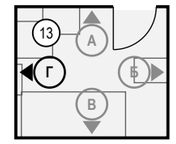

Ведомость отделки (на листе)

Марка	Поверхность	Материал, изделие	Цвет, код	Кол.
О8	стены	облицовка плиткой, Atlas Concorde Marvel Travertine, 600×1200×9 мм, А8UZ, затирка CG2WA	Atlas Concorde A8UZ «Marvel Travertine»	5 м²
О9	потолок	окраска, Tikkurila Luja 7, матовая, подготовка Q3	Little Greene No. 222 «Loft White»	5,3 м²

Визуализация этой стены — лист 111



Примечания


1. Размеры — в мм от чистовых поверхностей стен; условные обозначения и общие указания — лист 2.
2. Схема мебели, приборов и декора не является технической документацией для производства мебели; габариты — по паспортам изделий.
3. Выводы ВК — коды и высоты по листу выводов сантехники.
4. Облицовка — по сетке швов 2 мм, раскладка от оси стены (треугольник у пола), целые ряды от пола; подрезки — по листу раскладки плитки.
5. Гидроизоляция в 2 слоя, заход на стены 200 мм — до облицовки, с актом скрытых работ и тестом проливом (узел — на листе узлов).

					Проект: Дом 120 м²
	Лист	№ док.	Подпись	Дата	Развёртка стены Г. Санузел второго этажа (пом. 13)
Дизайнер	Кырлан А.С.			19.10.26	


Стадия	Лист	Листов
П	114	128

выпуск 19.10.2026 № 66b2a77b4d · стр. 114 из 128


Вид с фасадами

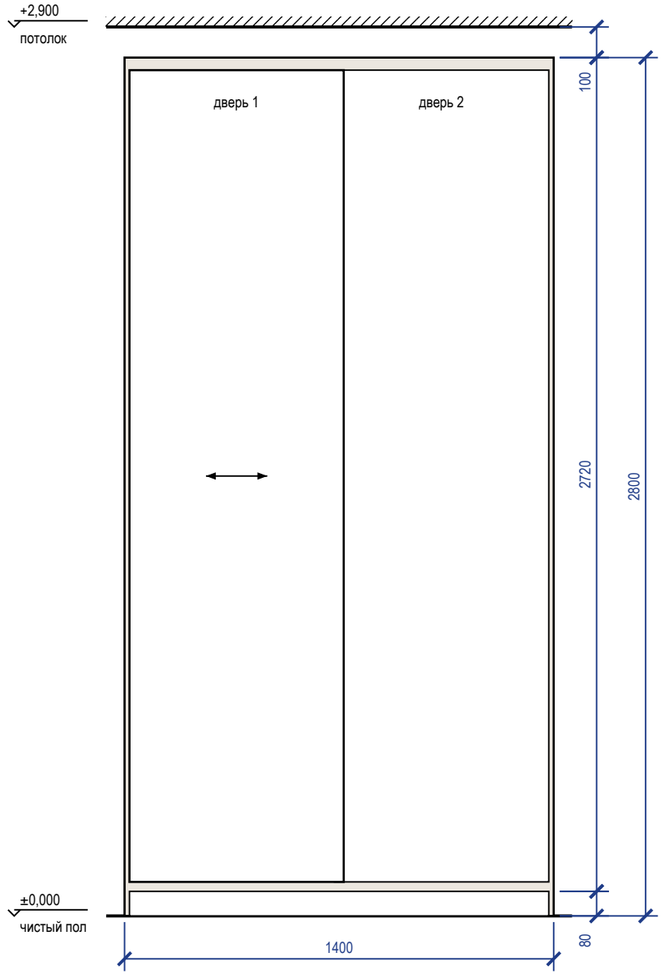


Вид без фасадов

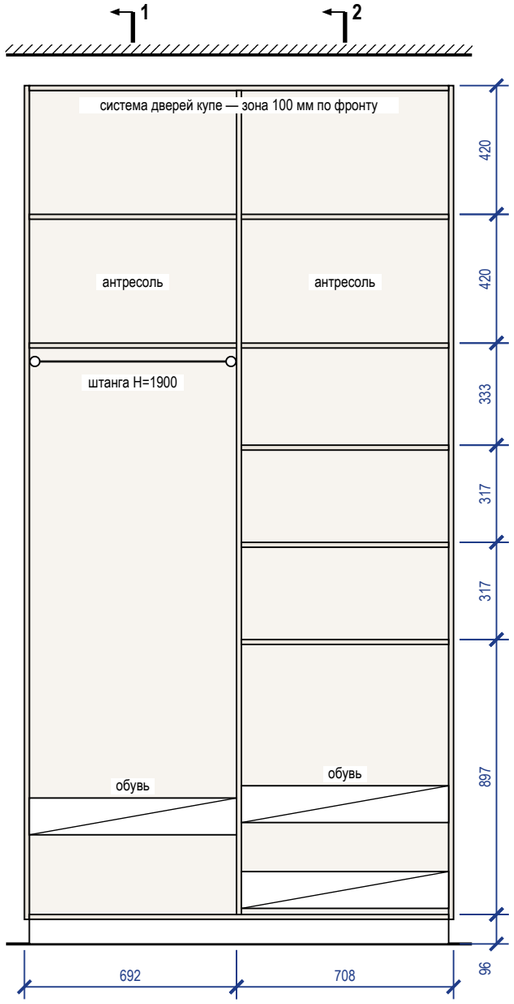

Разрез 1-1

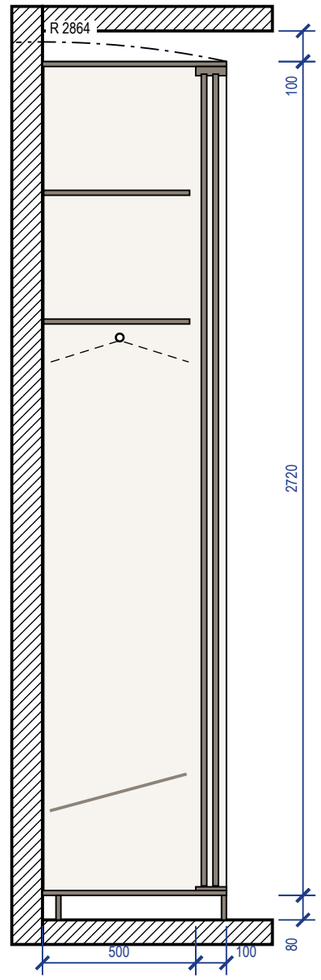


Разрез 2-2

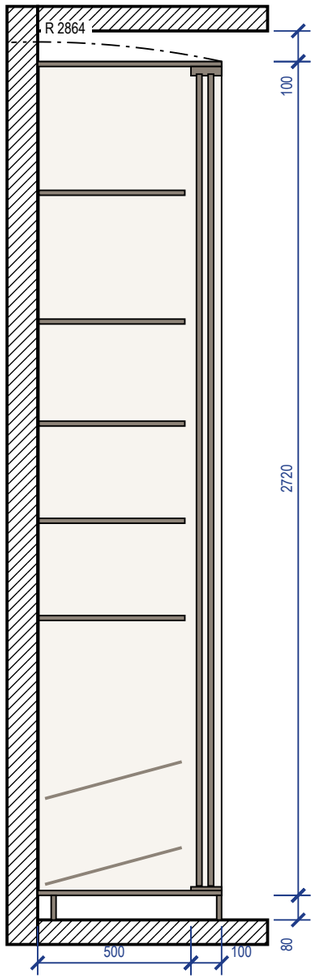

Примечания

1. Размеры — в мм по чистовой отделке; изделие 1400×600×2800 (Ш×Г×В). Перед раскроем — контрольный замер цеха после чистовой отделки стен, пола и потолка.
2. Корпус — ЛДСП 16 мм, задняя стенка ХДФ 4 мм в паз, цоколь 80 мм на регулируемых опорах; двери купе — ЛДСП 10 мм в алюминиевом профиле, нахлёст 30 мм, ширина двери 699 мм, высота — проём минус 40 мм; цвет — по колерной карте.
3. Кромка: скрытые торцы 0,4 мм, видимые 2 мм (ПВХ/АБС).
4. Номинальные зазоры: дверь купе — боковина 3 мм, фасад ящика — стойка 2 мм; ящики внутри купе — с накладкой 30 мм на стойке со стороны нахлёста дверей.
5. Ящики — направляющие полного выдвижения NL 450 (внутренняя глубина 496 мм ≥ NL + 3); присадка по 32-й системе — выполняет цех.
6. Зазор до потолка 100 мм — закрыть планкой в цвет корпуса при монтаже.
7. Подъём корпуса: диагональ боковины $\sqrt{(2800^2 + 600^2)} = 2864$ мм < 2900 мм до потолка — корпус собирается лёжа и поднимается поворотом.
8. Крепление к стене от опрокидывания — уголки 2 шт. к несущему основанию (монтажная схема шкафов).


3D орто

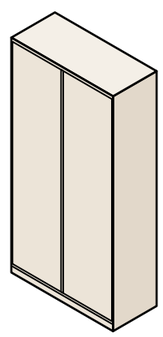


					Проект: Дом 120 м²	
	Лист	№ док.	Подпись	Дата	Шкаф-купе M_25	Стадия / Лист / Листов
Дизайнер	Кырлан А.С.			19.10.26		П / Д_1 / 128

выпуск 19.10.2026 № 66b2a77b4d · стр. 115 из 128


Вид с фасадами

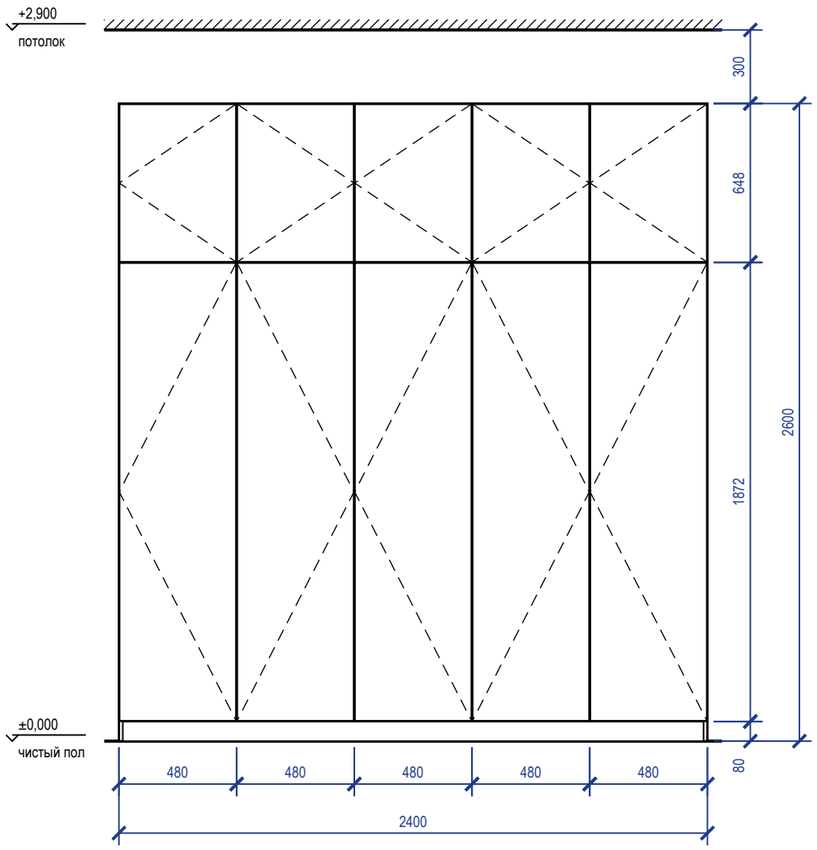


Вид без фасадов

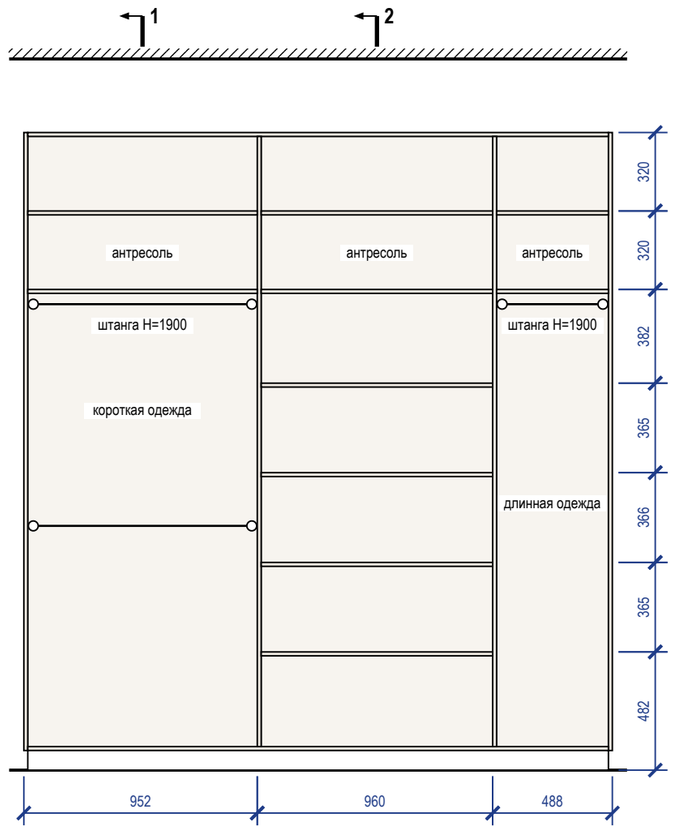

Разрез 1-1

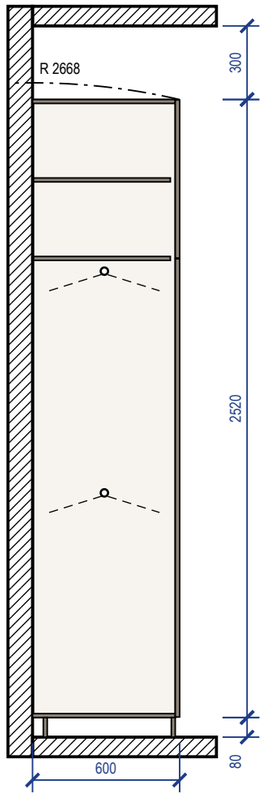


Разрез 2-2

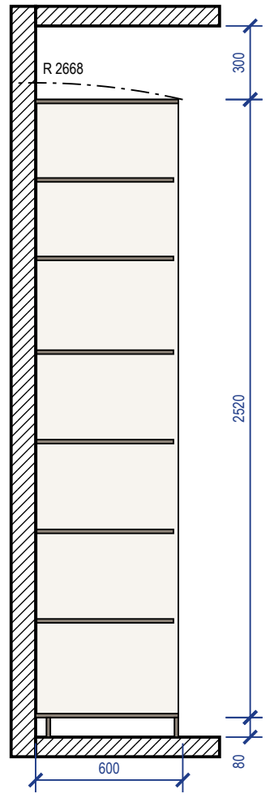

Примечания

1. Размеры — в мм по чистовой отделке; изделие 2400×600×2600 (Ш×Г×В). Перед раскроем — контрольный замер цеха после чистовой отделки стен, пола и потолка.
2. Корпус — ЛДСП 16 мм, задняя стенка ХДФ 4 мм в паз, цоколь 80 мм на регулируемых опорах; фасады — МДФ, эмаль матовая 18 мм накладные, цвет — по колерной карте; петли с доводчиком: фасад 1869 мм — 4 петли, фасад 645 мм — 2 петли.
3. Кромка: скрытые торцы 0,4 мм, видимые 2 мм (ПВХ/АБС).
4. Номинальные зазоры: между фасадами 3 мм, фасад — стена и фасад — потолок не менее 3 мм, фасад ящика — стойка 2 мм.
5. Ящики — направляющие полного выдвижения NL 550 (внутренняя глубина 578 мм ≥ NL + 3); присадка по 32-й системе — выполняет цех.
6. Зазор до потолка 300 мм.
7. Подъём корпуса: диагональ боковины $\sqrt{(2600^2 + 600^2)} = 2668$ мм < 2900 мм до потолка — корпус собирается лёжа и поднимается поворотом.
8. Крепление к стене от опрокидывания — уголки 2 шт. к несущему основанию (монтажная схема шкафов).

3D орто

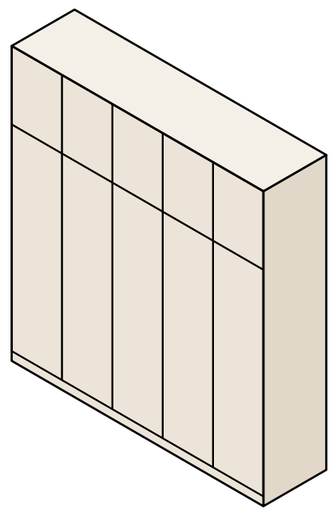


					Проект: Дом 120 м²
	Лист	№ док.	Подпись	Дата	
Дизайнер	Кырлан А.С.			19.10.26	Шкаф распашной M_30


Стадия	Лист	Листов
П	Д_2	128

выпуск 19.10.2026 № 66b2a77b4d · стр. 116 из 128


Вид с фасадами

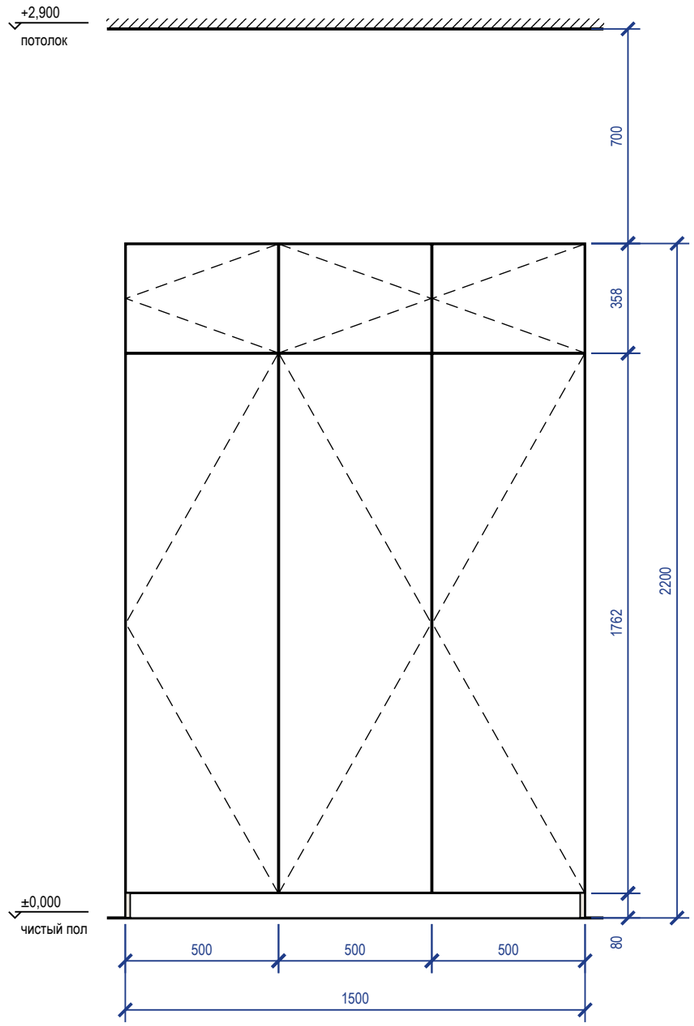


Вид без фасадов

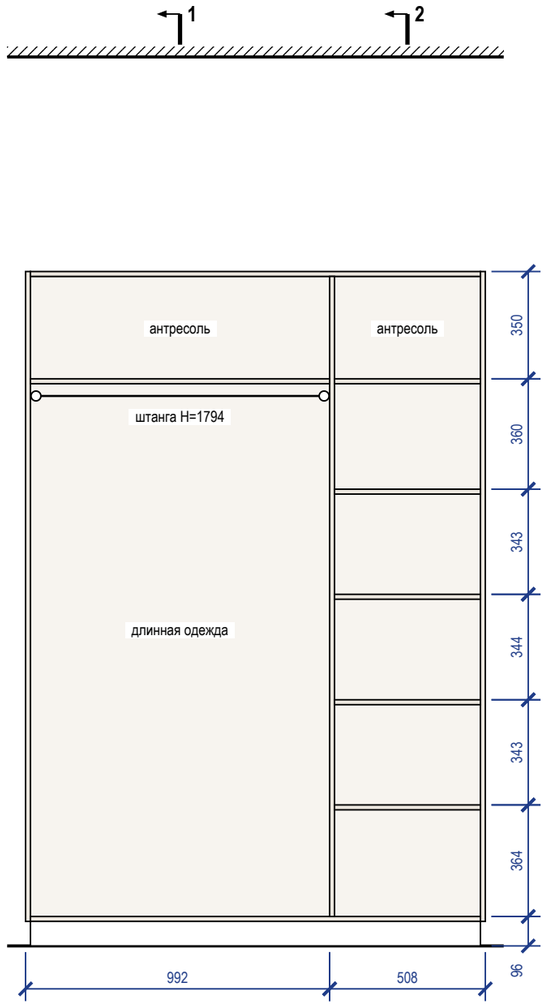

Разрез 1-1

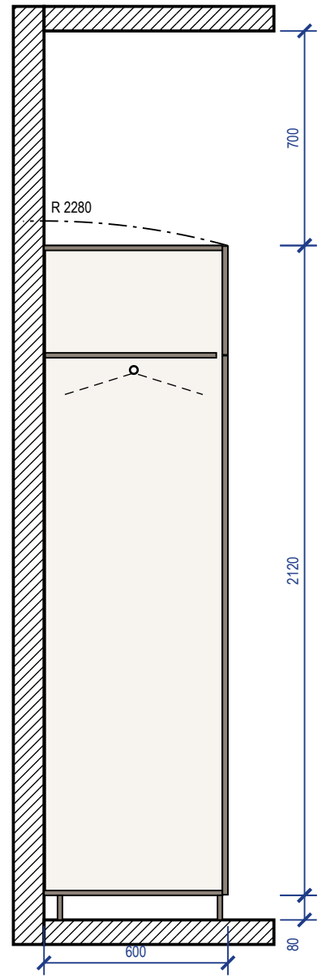


Разрез 2-2

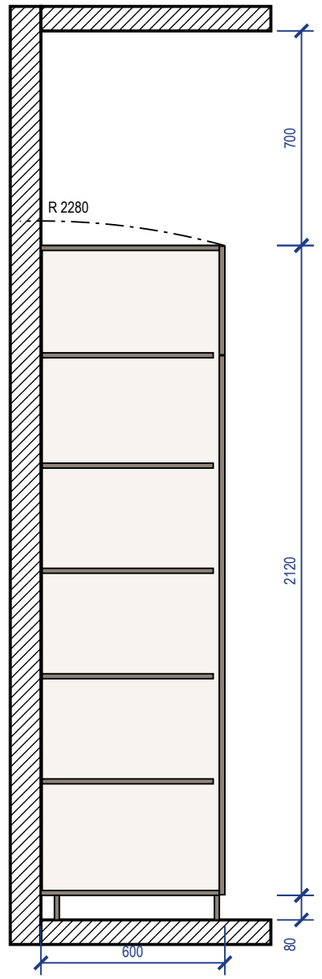

Примечания

1. Размеры — в мм по чистовой отделке; изделие 1500×600×2200 (Ш×Г×В). Перед раскроем — контрольный замер цеха после чистовой отделки стен, пола и потолка.
2. Корпус — ЛДСП 16 мм, задняя стенка ХДФ 4 мм в паз, цоколь 80 мм на регулируемых опорах; фасады — МДФ, эмаль матовая 18 мм накладные, цвет — по колерной карте; петли с доводчиком: фасад 1759 мм — 4 петли, фасад 355 мм — 2 петли.
3. Кромка: скрытые торцы 0,4 мм, видимые 2 мм (ПВХ/АБС).
4. Номинальные зазоры: между фасадами 3 мм, фасад — стена и фасад — потолок не менее 3 мм, фасад ящика — стойка 2 мм.
5. Ящики — направляющие полного выдвижения NL 550 (внутренняя глубина 578 мм ≥ NL + 3); присадка по 32-й системе — выполняет цех.
6. Зазор до потолка 700 мм.
7. Подъём корпуса: диагональ боковины $\sqrt{(2200^2 + 600^2)} = 2280$ мм < 2900 мм до потолка — корпус собирается лёжа и поднимается поворотом.
8. Крепление к стене от опрокидывания — уголки 2 шт. к несущему основанию (монтажная схема шкафов).


3D орто

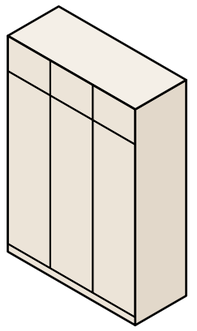


					Проект: Дом 120 м²		
	Лист	№ док.	Подпись	Дата			
Дизайнер	Кырлан А.С.			19.10.26	Шкаф распашной М_35	Стадия	Лист	Листов
						П	Д_3	128

выпуск 19.10.2026 № 66b2a77b4d · стр. 117 из 128


Общий вид

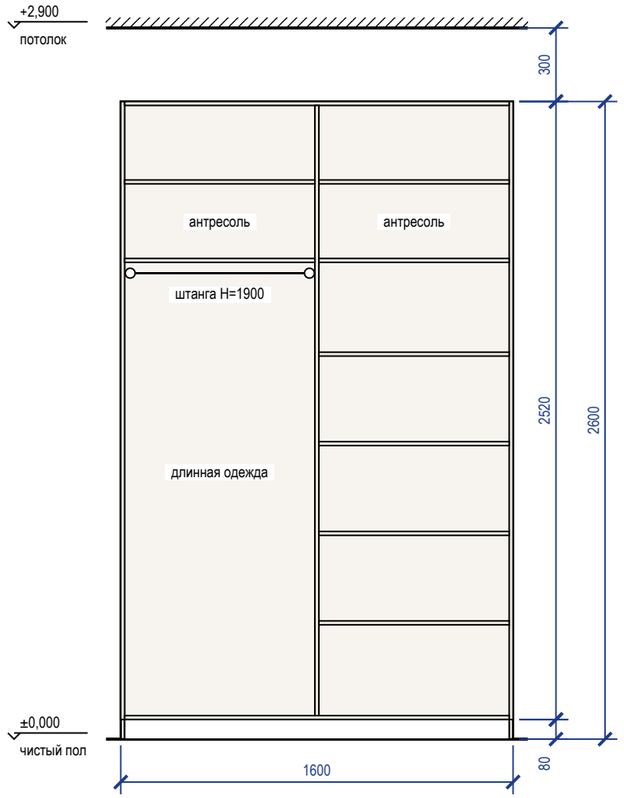


Наполнение, размеры в свету

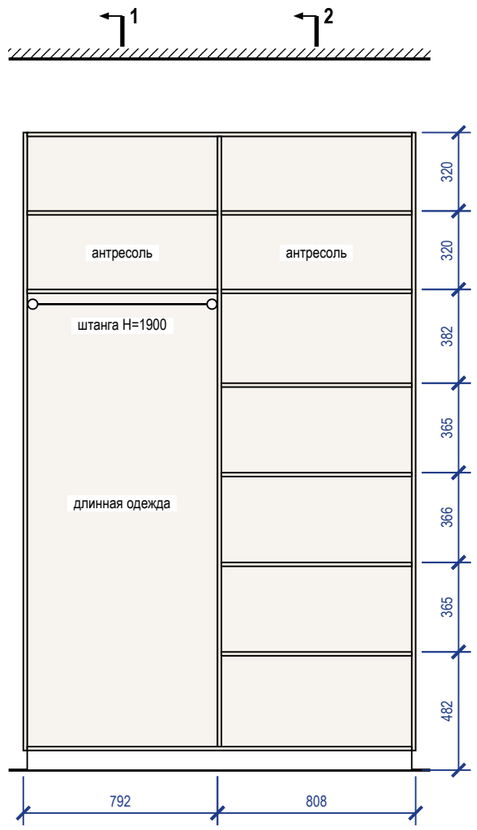

Разрез 1-1

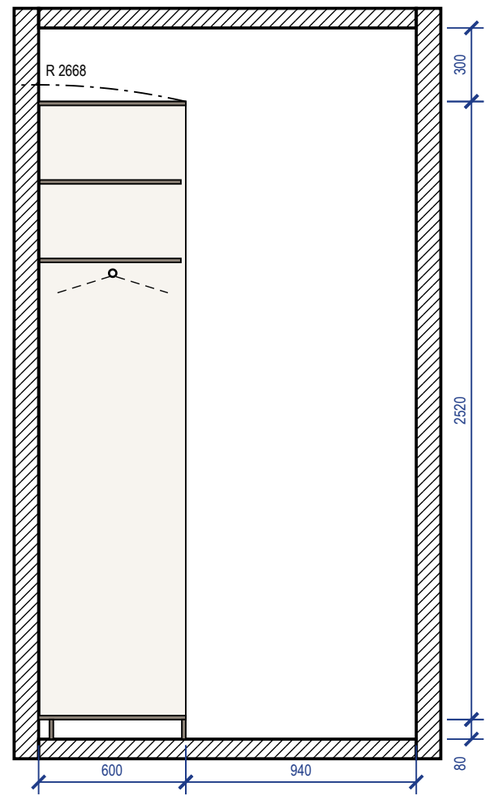


Разрез 2-2

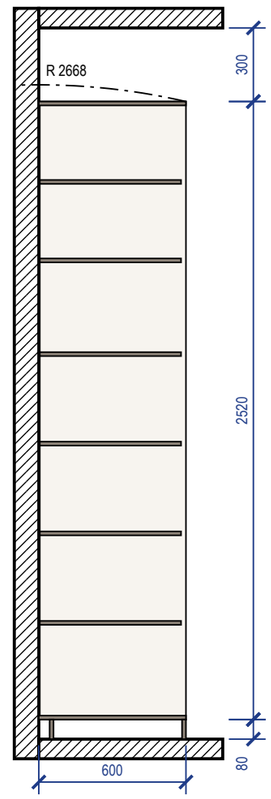

Примечания

1. Размеры — в мм по чистовой отделке; изделие 1600×600×2600 (Ш×Г×В). Перед раскроем — контрольный замер цеха после чистовой отделки стен, пола и потолка.
2. Корпус — ЛДСП 16 мм, задняя стенка ХДФ 4 мм в паз, цоколь 80 мм на регулируемых опорах; открытая система без фасадов, ящики с фасадами.
3. Кромка: скрытые торцы 0,4 мм, видимые 2 мм (ПВХ/АБС).
4. Номинальные зазоры: между фасадами ящиков 3 мм, фасад ящика — стойка 2 мм.
5. Ящики — направляющие полного выдвижения NL 550 (внутренняя глубина 596 мм ≥ NL + 3); присадка по 32-й системе — выполняет цех.
6. Зазор до потолка 300 мм.
7. Подъём корпуса: диагональ боковины $\sqrt{(2600^2 + 600^2)} = 2668$ мм < 2900 мм до потолка — корпус собирается лёжа и поднимается поворотом.
8. Крепление к стене от опрокидывания: true; основание стены и шаг анкеров — монтажная схема шкафов.
9. Проход перед изделием 940 мм показан на разрезе 1-1.

3D орто

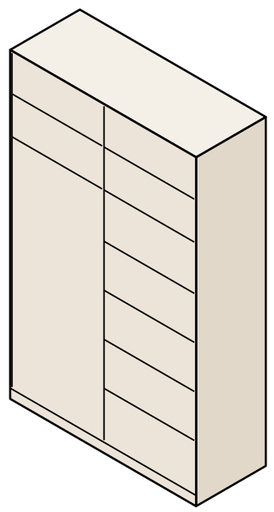


					Проект: Дом 120 м²
	Лист	№ док.	Подпись	Дата	
Дизайнер	Кырлан А.С.			19.10.26	Система хранения M_38


Стадия	Лист	Листов
П	Д_4	128

выпуск 19.10.2026 № 66b2a77b4d · стр. 118 из 128


Общий вид

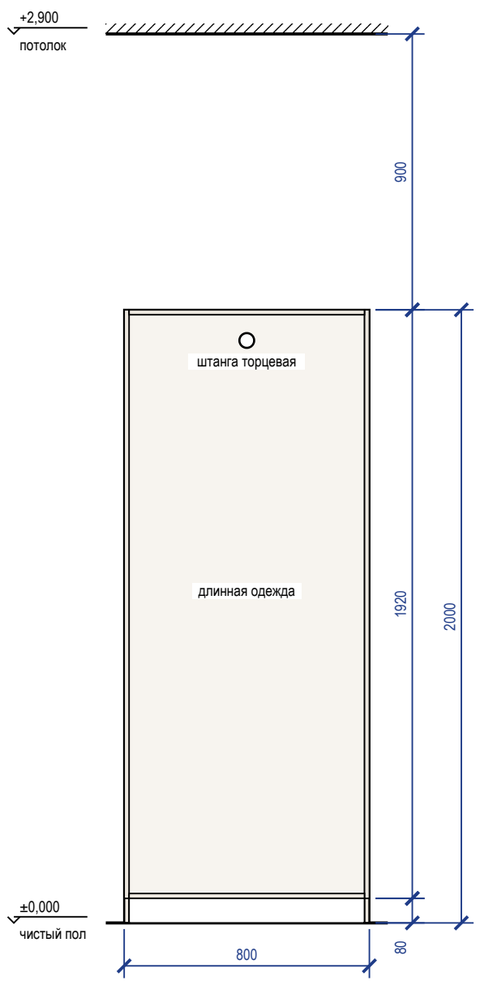

Наполнение, размеры в свету

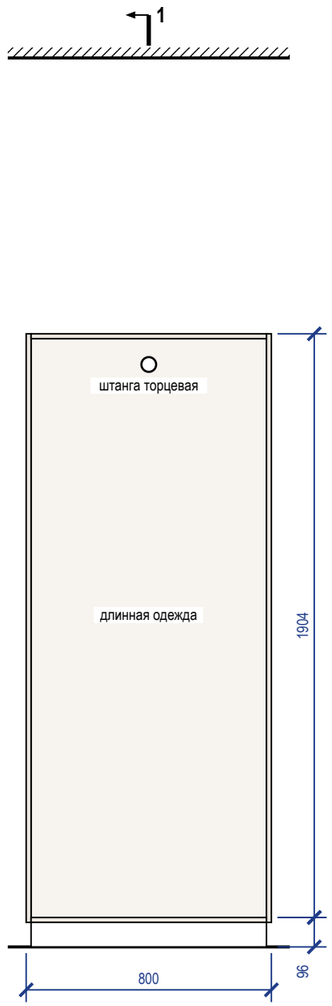


Разрез 1-1

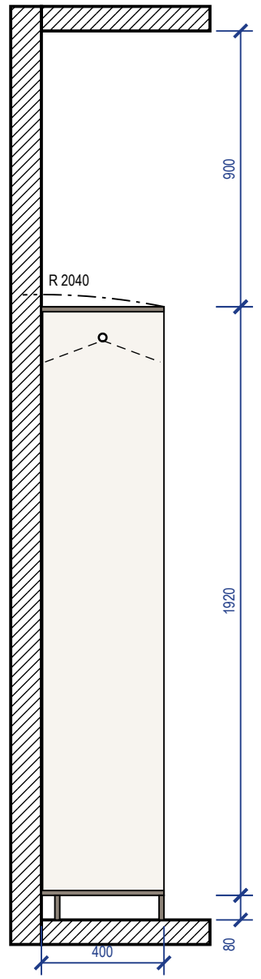

Примечания

1. Размеры — в мм по чистовой отделке; изделие 800×400×2000 (Ш×Г×В). Перед раскроем — контрольный замер цеха после чистовой отделки стен, пола и потолка.
2. Корпус — ЛДСП 16 мм, задняя стенка ХДФ 4 мм в паз, цоколь 80 мм на регулируемых опорах; открытая система без фасадов, ящики с фасадами.
3. Кромка: скрытые торцы 0,4 мм, видимые 2 мм (ПВХ/АБС).
4. Номинальные зазоры: между фасадами ящиков 3 мм, фасад ящика — стойка 2 мм.
5. Ящики — направляющие полного выдвижения NL 350 (внутренняя глубина 396 мм ≥ NL + 3); присадка по 32-й системе — выполняет цех.
6. Зазор до потолка 900 мм.
7. Подъём корпуса: диагональ боковины $\sqrt{(2000^2 + 400^2)} = 2040$ мм < 2900 мм до потолка — корпус собирается лёжа и поднимается поворотом.
8. Крепление к стене от опрокидывания: true; основание стены и шаг анкеров — монтажная схема шкафов.


3D орто

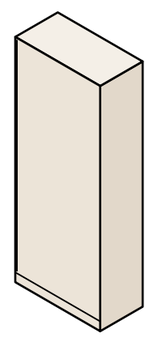


					Проект: Дом 120 м²		
	Лист	№ док.	Подпись	Дата	Система хранения M_39	Стадия	Лист	Листов
Дизайнер	Кырлан А.С.			19.10.26		П	Д_5	128

выпуск 19.10.2026 № 66b2a77b4d · стр. 119 из 128


Общий вид

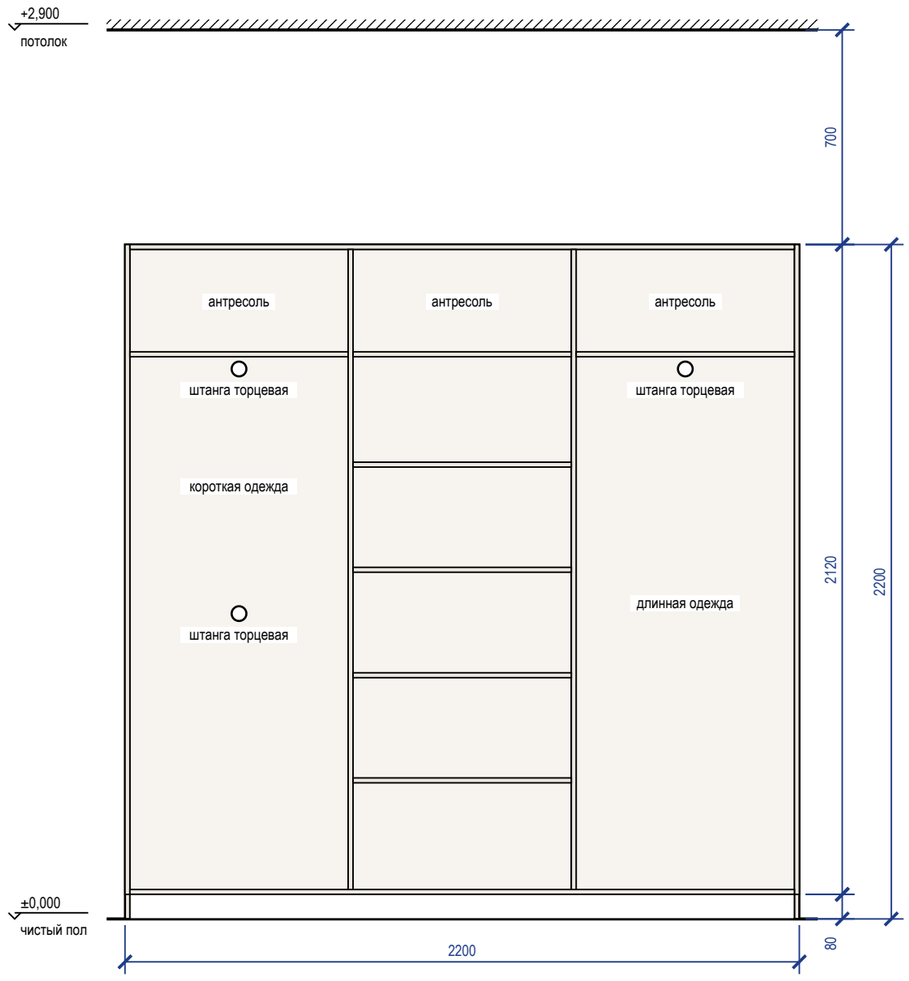


Наполнение, размеры в свету

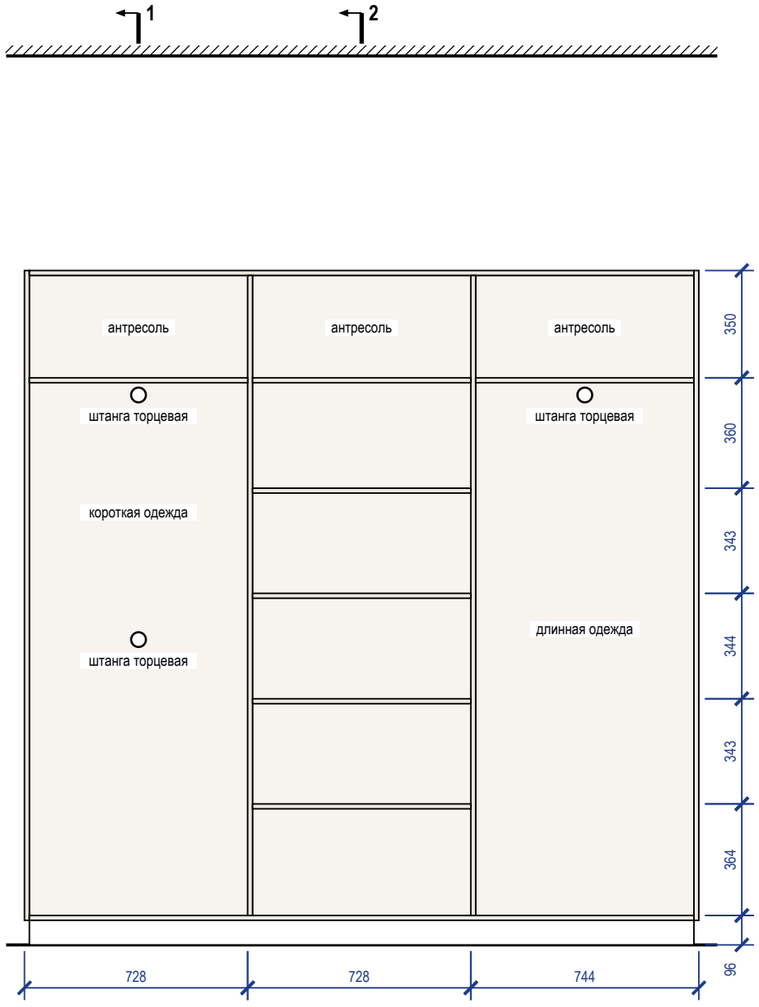

Разрез 1-1

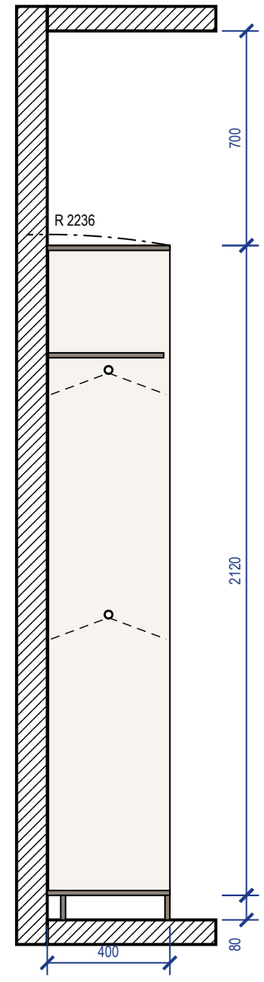


Разрез 2-2

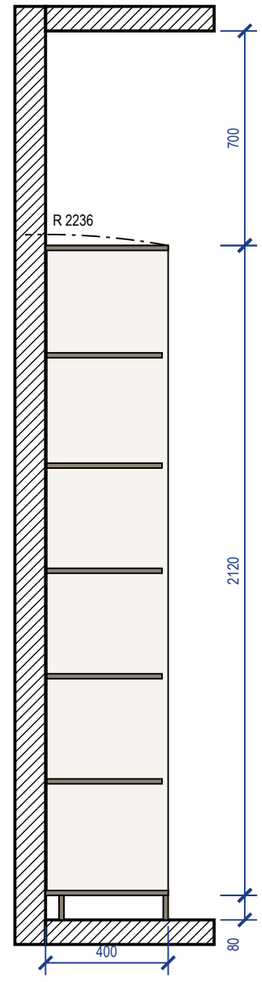

Примечания

1. Размеры — в мм по чистовой отделке; изделие 2200×400×2200 (Ш×Г×В). Перед раскроем — контрольный замер цеха после чистовой отделки стен, пола и потолка.
2. Корпус — ЛДСП 16 мм, задняя стенка ХДФ 4 мм в паз, цоколь 80 мм на регулируемых опорах; открытая система без фасадов, ящики с фасадами.
3. Кромка: скрытые торцы 0,4 мм, видимые 2 мм (ПВХ/АБС).
4. Номинальные зазоры: между фасадами ящиков 3 мм, фасад ящика — стойка 2 мм.
5. Ящики — направляющие полного выдвижения NL 350 (внутренняя глубина 396 мм ≥ NL + 3); присадка по 32-й системе — выполняет цех.
6. Зазор до потолка 700 мм.
7. Подъём корпуса: диагональ боковины $\sqrt{(2200^2 + 400^2)} = 2236$ мм < 2900 мм до потолка — корпус собирается лёжа и поднимается поворотом.
8. Крепление к стене от опрокидывания: true; основание стены и шаг анкеров — монтажная схема шкафов.

3D орто

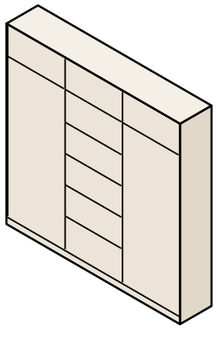


					Проект: Дом 120 м²
	Лист	№ док.	Подпись	Дата	Система хранения M_40
Дизайнер	Кырлан А.С.			19.10.26	


Стадия	Лист	Листов
П	Д_6	128

выпуск 19.10.2026 № 66b2a77b4d · стр. 120 из 128


Общий вид

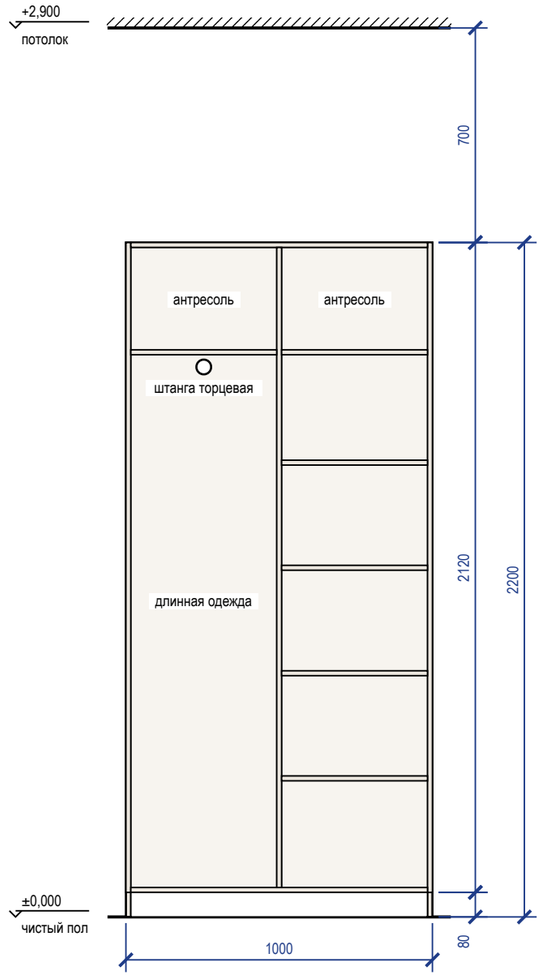


Наполнение, размеры в свету

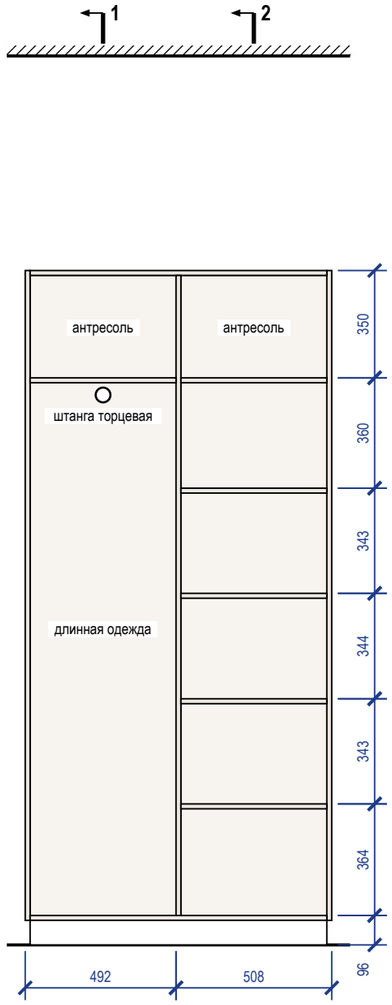

Разрез 1-1

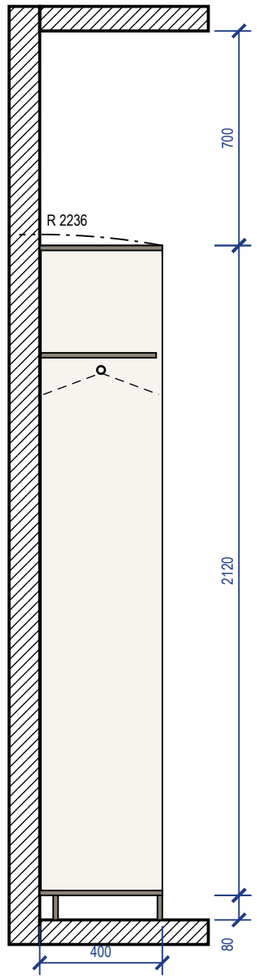


Разрез 2-2

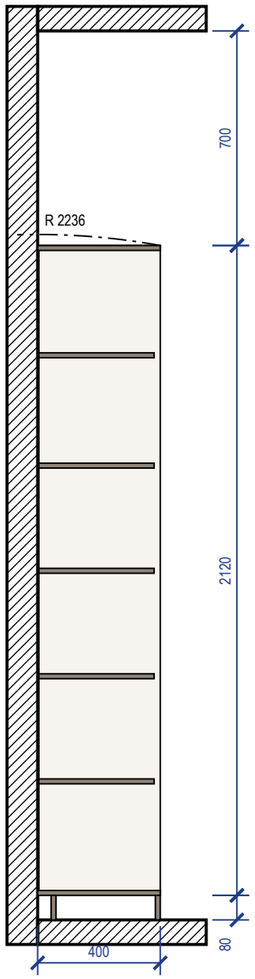

Примечания

1. Размеры — в мм по чистовой отделке; изделие 1000×400×2200 (Ш×Г×В). Перед раскроем — контрольный замер цеха после чистовой отделки стен, пола и потолка.
2. Корпус — ЛДСП 16 мм, задняя стенка ХДФ 4 мм в паз, цоколь 80 мм на регулируемых опорах; открытая система без фасадов, ящики с фасадами.
3. Кромка: скрытые торцы 0,4 мм, видимые 2 мм (ПВХ/АБС).
4. Номинальные зазоры: между фасадами ящиков 3 мм, фасад ящика — стойка 2 мм.
5. Ящики — направляющие полного выдвижения NL 350 (внутренняя глубина 396 мм ≥ NL + 3); присадка по 32-й системе — выполняет цех.
6. Зазор до потолка 700 мм.
7. Подъём корпуса: диагональ боковины $\sqrt{(2200^2 + 400^2)} = 2236$ мм < 2900 мм до потолка — корпус собирается лёжа и поднимается поворотом.
8. Крепление к стене от опрокидывания: true; основание стены и шаг анкеров — монтажная схема шкафов.


3D орто

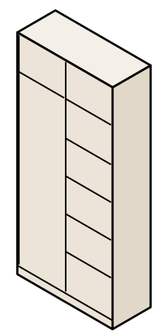


					Проект: Дом 120 м²	
	Лист	№ док.	Подпись	Дата	Система хранения M_41	Стадия / Лист / Листов
Дизайнер	Кырлан А.С.			19.10.26		П / Д_7 / 128

выпуск 19.10.2026 № 66b2a77b4d · стр. 121 из 128


Вид с фасадами

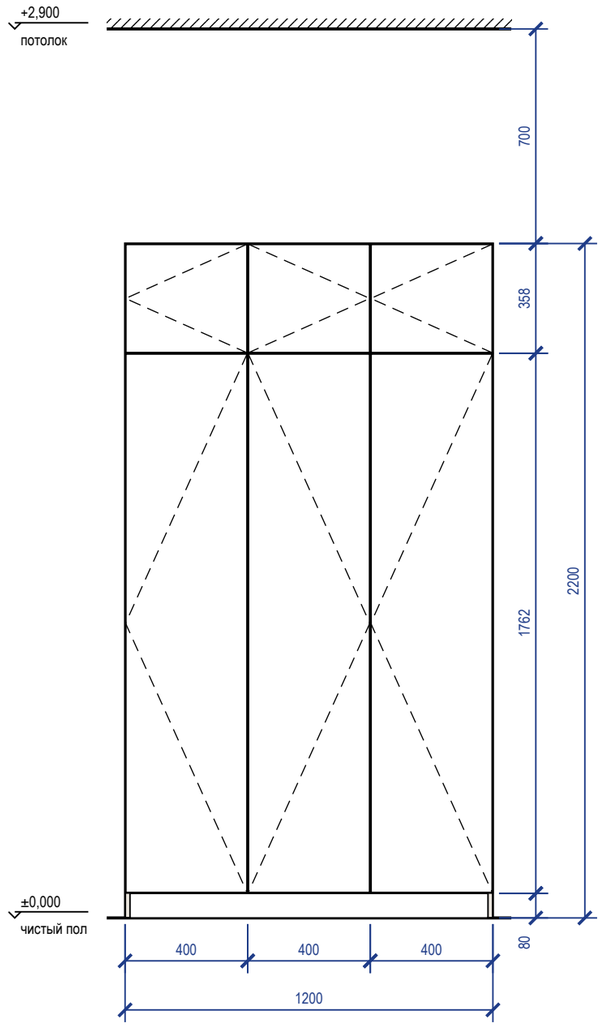


Вид без фасадов

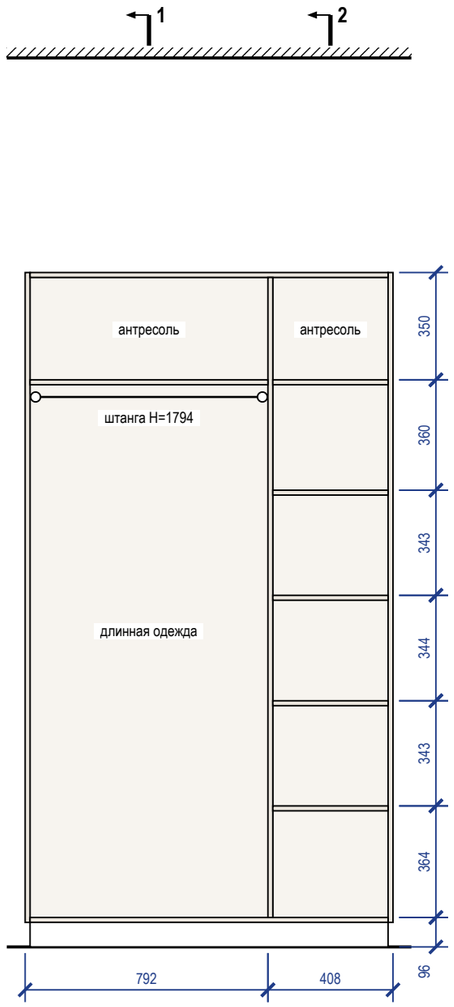

Разрез 1-1

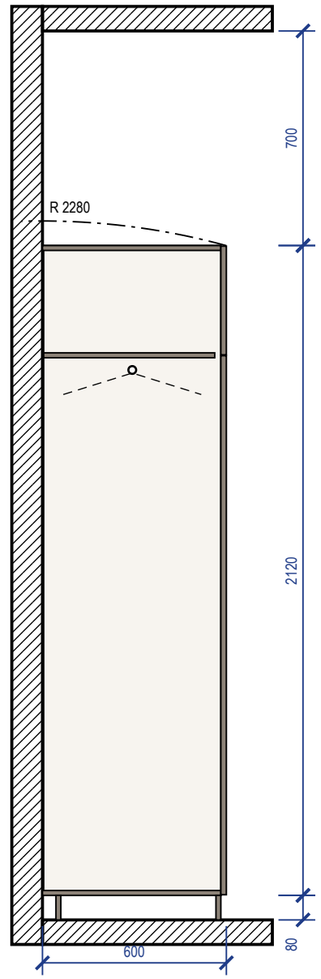


Разрез 2-2

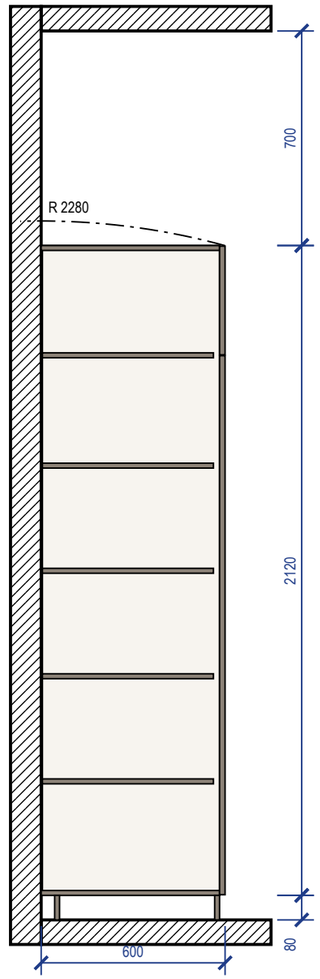

Примечания

1. Размеры — в мм по чистовой отделке; изделие 1200×600×2200 (Ш×Г×В). Перед раскроем — контрольный замер цеха после чистовой отделки стен, пола и потолка.
2. Корпус — ЛДСП 16 мм, задняя стенка ХДФ 4 мм в паз, цоколь 80 мм на регулируемых опорах; фасады — МДФ, эмаль матовая 18 мм накладные, цвет — по колерной карте; петли с доводчиком: фасад 1759 мм — 4 петли, фасад 355 мм — 2 петли.
3. Кромка: скрытые торцы 0,4 мм, видимые 2 мм (ПВХ/АБС).
4. Номинальные зазоры: между фасадами 3 мм, фасад — стена и фасад — потолок не менее 3 мм, фасад ящика — стойка 2 мм.
5. Ящики — направляющие полного выдвижения NL 550 (внутренняя глубина 578 мм ≥ NL + 3); присадка по 32-й системе — выполняет цех.
6. Зазор до потолка 700 мм.
7. Подъём корпуса: диагональ боковины $\sqrt{(2200^2 + 600^2)} = 2280$ мм < 2900 мм до потолка — корпус собирается лёжа и поднимается поворотом.
8. Крепление к стене от опрокидывания — уголки 2 шт. к несущему основанию (монтажная схема шкафов).


3D орто

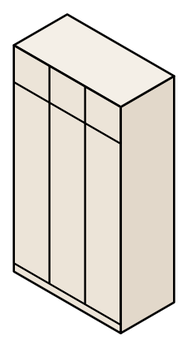


					Проект: Дом 120 м²	
	Лист	№ док.	Подпись	Дата		
Дизайнер	Кырлан А.С.			19.10.26	Шкаф распашной М_45	Стадия / Лист / Листов
						П / Д_8 / 128

выпуск 19.10.2026 № 66b2a77b4d · стр. 122 из 128


Общий вид

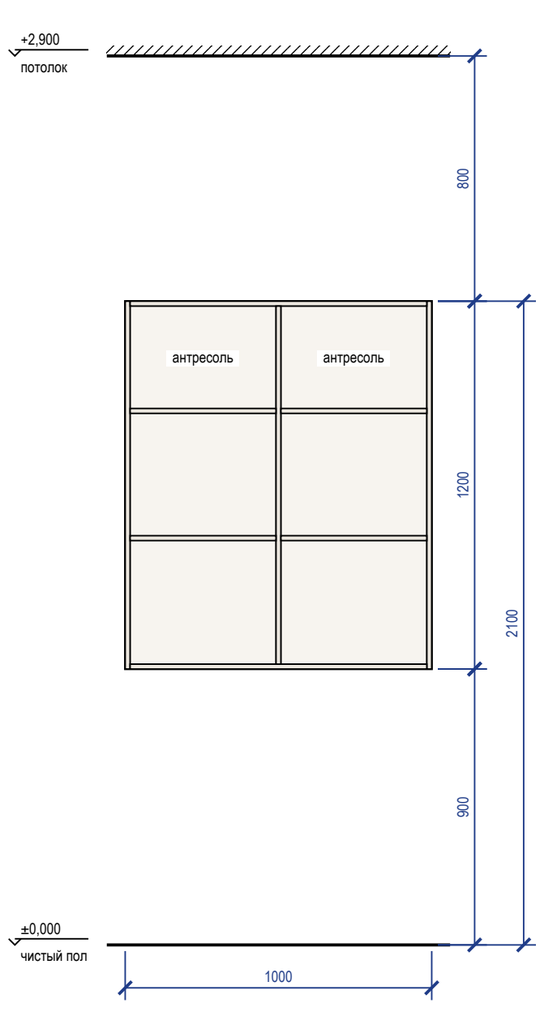

Наполнение, размеры в свету

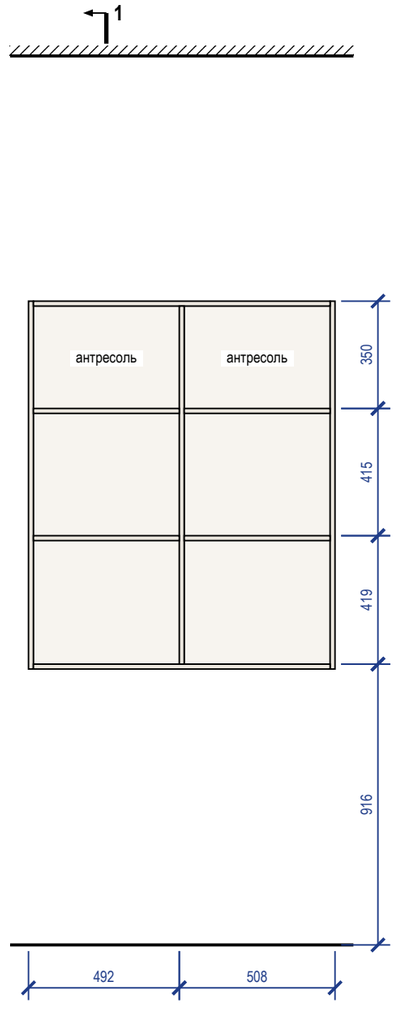


Разрез 1-1

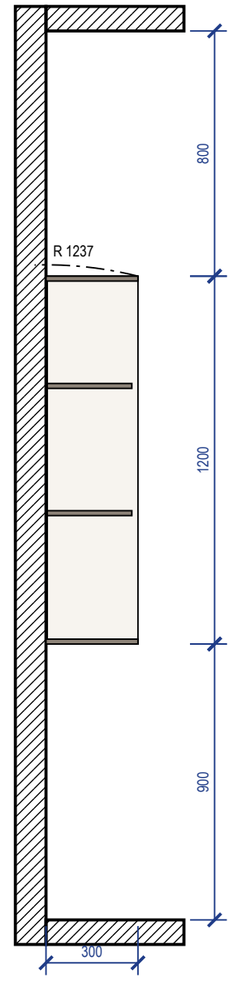

Примечания

1. Размеры — в мм по чистовой отделке; изделие 1000×300×1200 (Ш×Г×В). Перед раскроем — контрольный замер цеха после чистовой отделки стен, пола и потолка.
2. Корпус — ЛДСП 16 мм, задняя стенка ХДФ 4 мм в паз, цоколь 0 мм на регулируемых опорах; открытая система без фасадов, ящики с фасадами.
3. Кромка: скрытые торцы 0,4 мм, видимые 2 мм (ПВХ/АБС).
4. Номинальные зазоры: между фасадами ящиков 3 мм, фасад ящика — стойка 2 мм.
5. Ящики — направляющие полного выдвижения NL 270 (внутренняя глубина 296 мм ≥ NL + 3); присадка по 32-й системе — выполняет цех.
6. Зазор до потолка 800 мм.
7. Подъём корпуса: диагональ боковины $\sqrt{(1200^2 + 300^2)} = 1237$ мм < 2000 мм до потолка — корпус собирается лёжа и поднимается поворотом.
8. Крепление к стене от опрокидывания: true; основание стены и шаг анкеров — монтажная схема шкафов.


3D орто

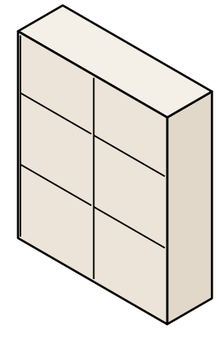


					Проект: Дом 120 м²	
	Лист	№ док.	Подпись	Дата		
Дизайнер	Кырлан А.С.			19.10.26	Система хранения M_47	Стадия: П; Лист: Д_9; Листов: 128

выпуск 19.10.2026 № 66b2a77b4d · стр. 123 из 128


Вид с фасадами

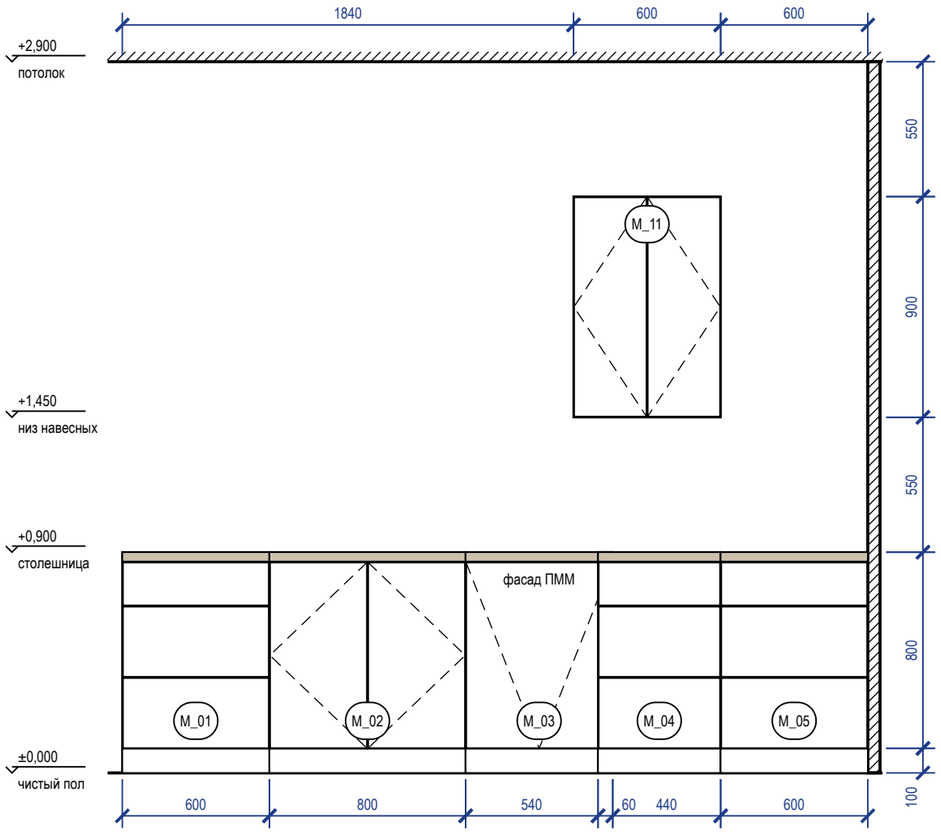


Вид без фасадов (наполнение, выводы)

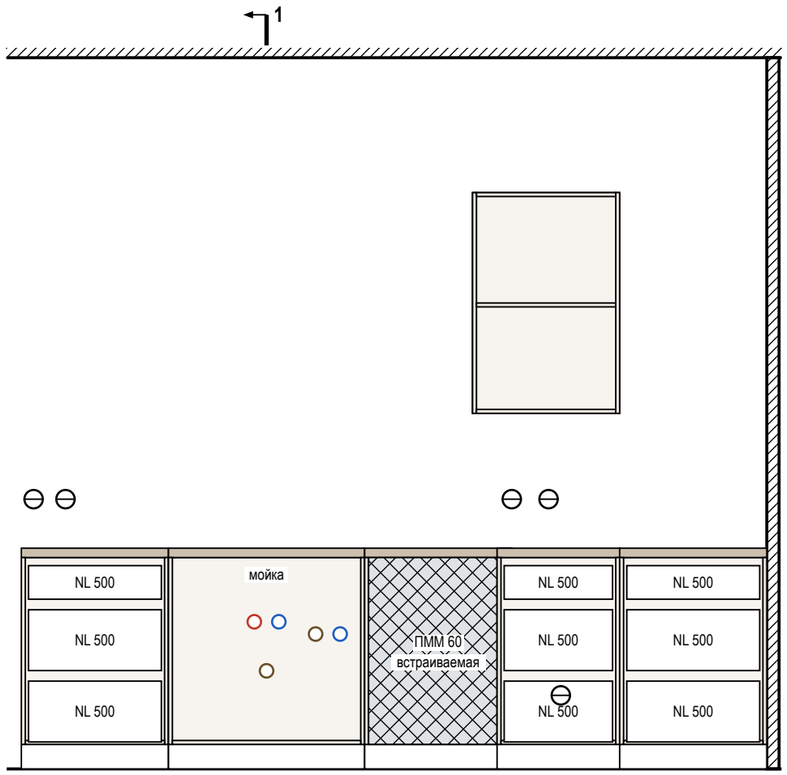

Разрез 1-1

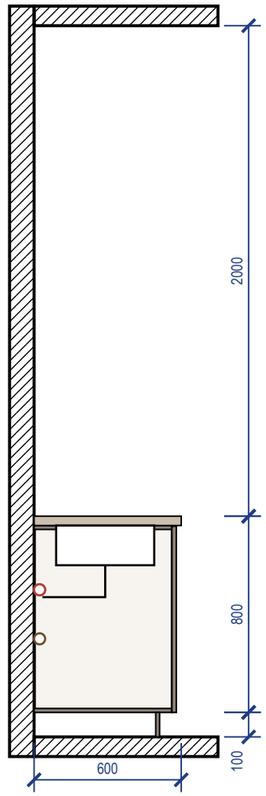

3D орто

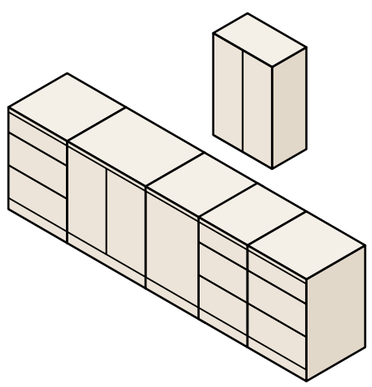

Примечания


1. Размеры — в мм по чистовой отделке, вид из помещения; марки — как на плане расстановки. Перед раскроем — контрольный замер цеха после фартука и пола.
2. Корпуса — ЛДСП 16 мм, задняя стенка ХДФ 4 мм; фасады — МДФ, эмаль матовая 18 мм, цвет по колерной карте; столешница 38 мм, свес 20 мм; цоколь 100 мм.
3. Кромка: скрытые торцы 0,4 мм, видимые 2 мм. Номинальные зазоры: между фасадами 3 мм, фасад — столешница 3 мм, фасад — стена не менее 3 мм.
4. Ящики полного выдвижения и петли — с доводчиком; присадка по 32-й системе — выполняет цех.
5. Ниши техники — по монтажным схемам выбранных моделей: решётка в цоколе и канал за пеналом холодильника, зазор за духовым шкафом, фасад ПММ на двери машины.

					Проект: Дом 120 м²
	Лист	№ док.	Подпись	Дата	Кухня (пом. 1). Развёртка гарнитура
Дизайнер	Кырлан А.С.			19.10.26	


Стадия	Лист	Листов
П	Д_10	128

выпуск 19.10.2026 № 66b2a77b4d · стр. 124 из 128


Вид с фасадами

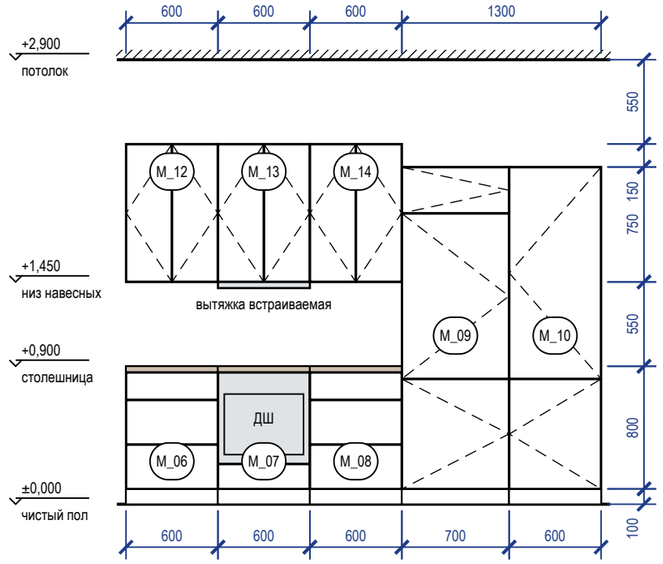


Вид без фасадов (наполнение, выводы)

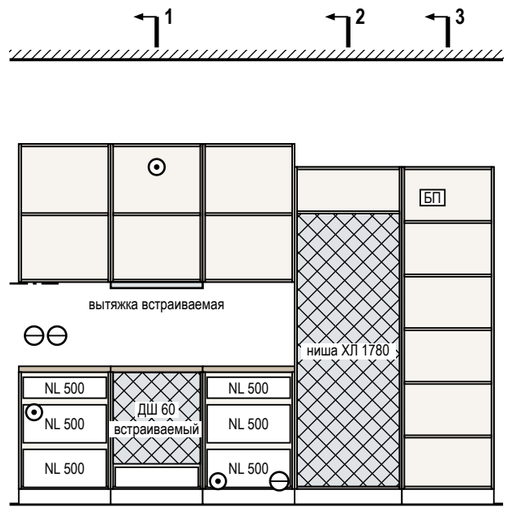


Разрез 1-1

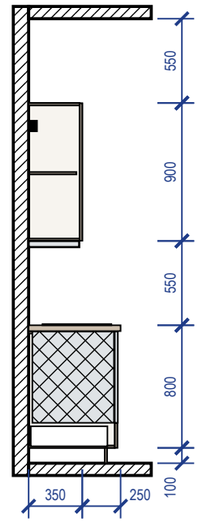


Разрез 2-2

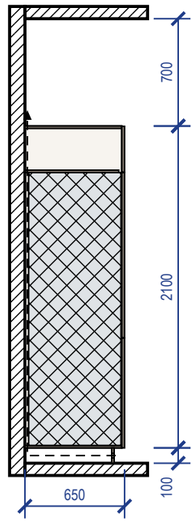

Разрез 3-3

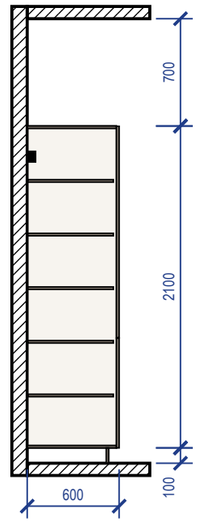

3D орто

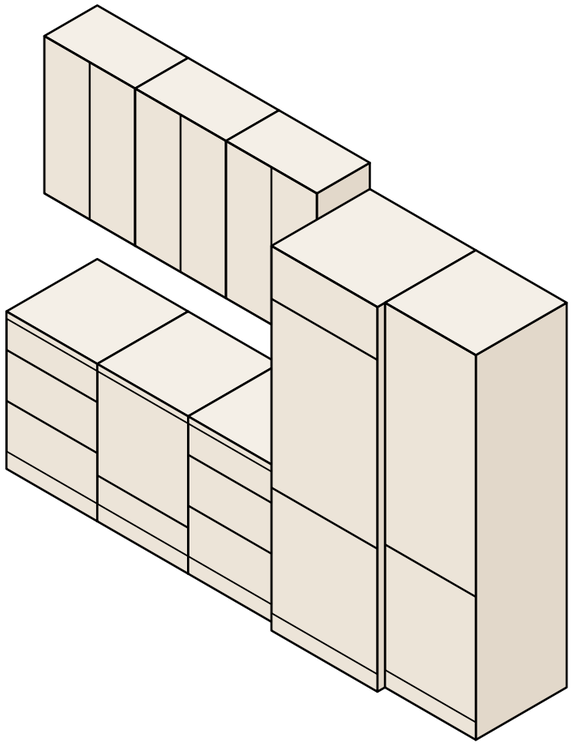

Примечания

1. Размеры — в мм по чистовой отделке, вид из помещения; марки — как на плане расстановки. Перед раскроем — контрольный замер цеха после фартука и пола.
2. Корпуса — ЛДСП 16 мм, задняя стенка ХДФ 4 мм; фасады — МДФ, эмаль матовая 18 мм, цвет по колерной карте; столешница 38 мм, свес 20 мм; цоколь 100 мм.
3. Кромка: скрытые торцы 0,4 мм, видимые 2 мм. Номинальные зазоры: между фасадами 3 мм, фасад — столешница 3 мм, фасад — стена не менее 3 мм.
4. Ящики полного выдвижения и петли — с доводчиком; присадка по 32-й системе — выполняет цех.
5. Вытяжка встраивается в навесной модуль над варочной: её низ 510 мм над панелью — меньше 650 мм, модуль поднять или принять вытяжку с допуском по паспорту модели.
6. Ниши техники (холодильник — ориентир 1780 мм) — по монтажным схемам выбранных моделей: решётка в цоколе и канал за пеналом холодильника, зазор за духовым шкафом, фасад ПММ на двери машины.

					Проект: Дом 120 м²
	Лист	№ док.	Подпись	Дата	Кухня (пом. 1). Развёртка гарнитура
Дизайнер	Кырлан А.С.			19.10.26	

Стадия	Лист	Листов
П	Д_11	128

выпуск 19.10.2026 № 66b2a77b4d · стр. 125 из 128

Ведомость отделки помещений (форма 1 прил. А ГОСТ 21.501-2018). Лист 1 из 2

№	Наименование помещения	Потолок			Стены и перегородки			Низ стен (плинтус)			Пол		Примечание
		Вид отделки	Код цвета	S, м²	Вид отделки	Код цвета	S, м²	Вид отделки	Код цвета	L, м	Вид отделки	S, м²	
1	Гостиная-кухня 31,32 м²	Окраска, Tikkurila Anti-Reflex 2, глубокоматовая, 2 слоя, подготовка Q3	Little Greene No. 222	31,32	Окраска, Farrow & Ball Modern Emulsion, матовая, 2 слоя, подготовка Q3 Акцент — стена А: окраска, Farrow & Ball Modern Emulsion, матовая, 2 слоя, подготовка Q3 Фартук кухни (стена А, Б): облицовка керамогранитом, аналог: керамогранит под травертин, матовый, 1200×600×9 мм, клей C2 TE S1, затирка CG2WA	Tikkurila G503 NCS S 3050-R80B по артикулу	43,15 11,58 2,00	Плинтус МДФ h=80 мм, аналог: МДФ под покраску 80×16	Tikkurila G503	21,7	Инженерная доска, 1167-4250, 2100×127 мм, на клею; тип 1, отм. ЧП ±0,000	31,32	Н стен 2900 (до потолка); матовая моющаяся, класс 1 EN 13300 — осознанно вместо полуматовой; плинтус в цвет: стены
2	Холл с лестницей 15,51 м²	Окраска, Tikkurila Anti-Reflex 2, глубокоматовая, 2 слоя, подготовка Q3	Little Greene No. 222	15,51	Окраска, Farrow & Ball Modern Emulsion, матовая, 2 слоя, подготовка Q3	Tikkurila G503	34,65	Плинтус МДФ h=80 мм, аналог: МДФ под покраску 80×16	Tikkurila G503	11,1	Инженерная доска, 1167-4250, 2100×127 мм, на клею; тип 1, отм. ЧП ±0,000	15,51	Н стен 2900 (до потолка); матовая моющаяся, класс 1 EN 13300 — осознанно вместо полуматовой; плинтус в цвет: стены
3	Кабинет 11,00 м²	Окраска, Tikkurila Anti-Reflex 2, глубокоматовая, 2 слоя, подготовка Q3	Little Greene No. 222	11,00	Окраска, Farrow & Ball Modern Emulsion, матовая, 2 слоя, подготовка Q3 Акцент — стена А: окраска, Farrow & Ball Modern Emulsion, матовая, 2 слоя, подготовка Q3	Tikkurila G503 NCS S 5020-G90Y	23,97 10,85	Плинтус МДФ h=80 мм, аналог: МДФ под покраску 80×16	Tikkurila G503	12,6	Инженерная доска, 1167-4250, 2100×127 мм, на клею; тип 1, отм. ЧП ±0,000	11,00	Н стен 2900 (до потолка); плинтус в цвет: стены
4	Санузел гостевой 4,17 м²	Окраска, Tikkurila Luja 7, матовая, 2 слоя, подготовка Q3	Little Greene No. 222	4,17	Облицовка плиткой, A8UZ, 600×1200×9 мм, клей C2 TE S1, затирка CG2WA	Atlas Concorde A8UZ	17,40	нет			Керамогранит, A8UZ, 600×1200×9 мм; тип 2, отм. ЧП −0,015	4,17	Н стен 2915 (до потолка); гидроизоляция обмазочная, 2 слоя, с заведением на стены 200 мм (по пирогу пола); тест проливом и акт скрытых работ
5	Прихожая 12,20 м²	Окраска, Tikkurila Anti-Reflex 2, глубокоматовая, 2 слоя, подготовка Q3	Little Greene No. 222	12,20	Окраска, Farrow & Ball Modern Emulsion, матовая, 2 слоя, подготовка Q3	Tikkurila G503	43,20	Плинтус МДФ h=80 мм, аналог: МДФ под покраску 80×16	Tikkurila G503	14,0	Керамогранит, A8UZ, 600×1200×9 мм; тип 3, отм. ЧП ±0,000	12,20	Н стен 2900 (до потолка); матовая моющаяся, класс 1 EN 13300 — осознанно вместо полуматовой; плинтус в цвет: стены
6	Спальня родителей 17,17 м²	Окраска, Tikkurila Anti-Reflex 2, глубокоматовая, 2 слоя, подготовка Q3	Little Greene No. 222	17,17	Окраска, Farrow & Ball Modern Emulsion, матовая, 2 слоя, подготовка Q3 Акцент — стена А: окраска, Farrow & Ball Modern Emulsion, матовая, 2 слоя, подготовка Q3	Tikkurila G503 Farrow & Ball No. 89	35,79 8,15	Плинтус МДФ h=80 мм, аналог: МДФ под покраску 80×16	Tikkurila G503	15,9	Инженерная доска, 1167-4250, 2100×127 мм, на клею; тип 1, отм. ЧП ±0,000	17,17	Н стен 2900 (до потолка); плинтус в цвет: стены
7	Детская 12,30 м²	Окраска, Tikkurila Anti-Reflex 2, глубокоматовая, 2 слоя, подготовка Q3	Little Greene No. 222	12,30	Окраска, Farrow & Ball Modern Emulsion, матовая, 2 слоя, подготовка Q3 Акцент — стена А: окраска, Farrow & Ball Modern Emulsion, матовая, 2 слоя, подготовка Q3	Tikkurila G503 Farrow & Ball No. 66	26,07 10,85	Плинтус МДФ h=69 мм, SX165	Tikkurila G503	13,3	Инженерная доска, 1167-4250, 2100×127 мм, на клею; тип 1, отм. ЧП ±0,000	12,30	Н стен 2900 (до потолка); плинтус в цвет: стены
8	Гардеробная 3,82 м²	Окраска, Tikkurila Anti-Reflex 2, глубокоматовая, 2 слоя, подготовка Q3	Little Greene No. 222	3,82	Окраска, Tikkurila Harmony, матовая, 2 слоя, подготовка Q3	Little Greene No. 222	22,06	Плинтус МДФ h=80 мм, аналог: МДФ под покраску 80×16	Little Greene No. 222	7,4	Инженерная доска, 1167-4250, 2100×127 мм, на клею; тип 1, отм. ЧП ±0,000	3,82	Н стен 2900 (до потолка); плинтус в цвет: стены
9	Кладовая 4,66 м²	Окраска, Tikkurila, глубокоматовая	NCS S 0300-N	4,66	Окраска, Tikkurila, матовая, подготовка Q3	NCS S 0502-Y	23,61	Плинтус МДФ h=69 мм, SX165	NCS S 0300-N	7,9	Инженерная доска, 1167-4250, 2100×127 мм, на клею; тип 4, отм. ЧП ±0,000	4,66	Н стен 2900 (до потолка)
10	Холл второго этажа 15,51 м²	Окраска, Tikkurila Anti-Reflex 2, глубокоматовая, 2 слоя, подготовка Q3	Little Greene No. 222	15,51	Окраска, Farrow & Ball Modern Emulsion, матовая, 2 слоя, подготовка Q3	Tikkurila G503	34,65	Плинтус МДФ h=80 мм, аналог: МДФ под покраску 80×16	Tikkurila G503	11,1	Инженерная доска, 1167-4250, 2100×127 мм, на клею; тип 1, отм. ЧП ±0,000	15,51	Н стен 2900 (до потолка); матовая моющаяся, класс 1 EN 13300 — осознанно вместо полуматовой; плинтус в цвет: стены

Примечания

1. Ведомость продолжена на листе 2 из 2; итоги, сводка площадей и примечания — на последнем листе ведомости.

					Проект: Дом 120 м²
	Лист	№ док.	Подпись	Дата	Ведомость отделки помещений. Лист 1 из 2
Дизайнер	Кырлан А.С.			19.10.26	

Стадия	Лист	Листов
П	С1	128

выпуск 19.10.2026 № 66b2a77b4d · стр. 126 из 128


Поз.	Наименование и техническая характеристика	Тип, марка, обозначение документа	Код продукции	Поставщик	Ед. изм.	Кол.	Образец	Примечание
	Лакокрасочные материалы							
1	Краска интерьерная водно-дисперсионная акриловая для стен, матовая, класс мокрого истирания 1 по EN 13300, база A; цвет Tikkurila G503 «Calla», колеровка машинная	Farrow & Ball Modern Emulsion		Farrow & Ball	л	77,5		поз. К1 колерной карты; пом. 1, 2, 3, 5, 6, 7, 10, 11, 12; S = 284,9 м² × 2 сл. × 0,12 л/м² = 68,4 л, +10 % и 0,5 л на подкраску → ≥ 75,7 л; тара 15 × 5 л + 1 × 2,5 л
2	Краска интерьерная водно-дисперсионная акриловая для акцентных стен, матовая, класс мокрого истирания 1 по EN 13300, база C; цвет NCS S 3050-R80B «Эгейский синий», колеровка машинная	Farrow & Ball Modern Emulsion		Farrow & Ball	л	5		поз. К2 колерной карты; пом. 1; S = 11,6 м² × 2 сл. × 0,12 л/м² = 2,8 л, +10 % и 0,5 л на подкраску → ≥ 3,6 л; тара 1 × 5 л
3	Краска интерьерная водно-дисперсионная акриловая для потолков, глубокоматовая, класс мокрого истирания 2 по EN 13300, база A; цвет Little Greene No. 222 «Loft White», колеровка машинная	Tikkurila Anti-Reflex 2		Tikkurila	л	36		поз. К3 колерной карты; пом. 1, 2, 3, 5, 6, 7, 8, 10, 11, 12; S = 133,2 м² × 2 сл. × 0,12 л/м² = 32,0 л, +10 % и 0,5 л на подкраску → ≥ 35,7 л; тара 4 × 9 л
4	Краска интерьерная водно-дисперсионная акриловая для акцентных стен, матовая, класс мокрого истирания 1 по EN 13300, база C; цвет NCS S 5020-G90Y «Олива», колеровка машинная	Farrow & Ball Modern Emulsion		Farrow & Ball	л	5		поз. К5 колерной карты; пом. 3; S = 10,8 м² × 2 сл. × 0,12 л/м² = 2,6 л, +10 % и 0,5 л на подкраску → ≥ 3,4 л; тара 1 × 5 л
5	Краска интерьерная водно-дисперсионная акриловая для потолков, матовая, класс мокрого истирания 1 по EN 13300, база A; цвет Little Greene No. 222 «Loft White», колеровка машинная	Tikkurila Luja 7		Tikkurila	л	3,6		поз. К7 колерной карты; пом. 4, 13; S = 9,5 м² × 2 сл. × 0,12 л/м² = 2,3 л, +10 % и 0,5 л на подкраску → ≥ 3,0 л; тара 1 × 2,7 л + 1 × 0,9 л
6	Краска интерьерная водно-дисперсионная акриловая для акцентных стен, матовая, класс мокрого истирания 1 по EN 13300, база C; цвет Farrow & Ball No. 89 «Lulworth Blue — светлая морская лазурь», колеровка машинная	Farrow & Ball Modern Emulsion		Farrow & Ball	л	5		поз. К8 колерной карты; пом. 6; S = 8,1 м² × 2 сл. × 0,12 л/м² = 2,0 л, +10 % и 0,5 л на подкраску → ≥ 2,7 л; тара 1 × 5 л
7	Краска интерьерная водно-дисперсионная акриловая для акцентных стен, матовая, класс мокрого истирания 1 по EN 13300, база C; цвет Farrow & Ball No. 66 «India Yellow — охра / горчица итальянских фасадов», колеровка машинная	Farrow & Ball Modern Emulsion		Farrow & Ball	л	5		поз. К9 колерной карты; пом. 7; S = 10,8 м² × 2 сл. × 0,12 л/м² = 2,6 л, +10 % и 0,5 л на подкраску → ≥ 3,4 л; тара 1 × 5 л
8	Краска интерьерная водно-дисперсионная акриловая для стен, матовая, класс мокрого истирания 1 по EN 13300, база A; цвет Little Greene No. 222 «Loft White», колеровка машинная	Tikkurila Harmony		Tikkurila	л	7,2		поз. К11 колерной карты; пом. 8; S = 22,1 м² × 2 сл. × 0,12 л/м² = 5,3 л, +10 % и 0,5 л на подкраску → ≥ 6,3 л; тара 2 × 2,7 л + 2 × 0,9 л
9	Краска интерьерная водно-дисперсионная акриловая для стен, матовая, класс мокрого истирания 2 по EN 13300, база A; цвет NCS S 0502-Y, колеровка машинная	Tikkurila		Tikkurila	л	7,2		поз. К13 колерной карты; пом. 9; S = 23,6 м² × 2 сл. × 0,12 л/м² = 5,7 л, +10 % и 0,5 л на подкраску → ≥ 6,7 л; тара 2 × 2,7 л + 2 × 0,9 л
10	Краска интерьерная водно-дисперсионная для потолков, глубокоматовая, класс мокрого истирания 2 по EN 13300, база A; цвет NCS S 0300-N, колеровка машинная	Tikkurila		Tikkurila	л	1,8		поз. К14 колерной карты; пом. 9; S = 4,7 м² × 2 сл. × 0,12 л/м² = 1,1 л, +10 % и 0,5 л на подкраску → ≥ 1,7 л; тара 2 × 0,9 л
11	Краска интерьерная водно-дисперсионная акриловая для акцентных стен, матовая, класс мокрого истирания 1 по EN 13300, база C; цвет Tikkurila H440 «H440 Wave — бирюзово-голубая вода», колеровка машинная	Farrow & Ball Modern Emulsion		Farrow & Ball	л	2,5		поз. К16 колерной карты; пом. 12; S = 7,4 м² × 2 сл. × 0,12 л/м² = 1,8 л, +10 % и 0,5 л на подкраску → ≥ 2,5 л; тара 1 × 2,5 л
12	Краска для МДФ и дерева в цвет Tikkurila G503 «Calla» — окраска плинтуса; блеск не ниже блеска стен	марка не задана			л	2,9		поз. К4, К10; пом. 1, 2, 3, 5, 6, 7, 10, 11, 12; L = 116,5 м, S = 10,9 м² × 2 сл. × 0,12 л/м² + 10 %; продукт подобрать в веере Tikkurila
13	Краска для МДФ и дерева в цвет Little Greene No. 222 «Loft White» — окраска плинтуса; блеск не ниже блеска стен	марка не задана			л	0,5		поз. К12; пом. 8; L = 7,4 м, S = 0,7 м² × 2 сл. × 0,12 л/м² + 10 %; продукт подобрать в веере Little Greene
14	Акрил, полуматовая в цвет NCS S 0300-N — окраска плинтуса	аналог по характеристикам			л	0,5		поз. К15; пом. 9; L = 7,9 м, S = 0,7 м² × 2 сл. × 0,12 л/м² + 10 %; продукт подобрать в веере NCS
15	Грунтовка акриловая под окраску стен и потолков — из системы производителя краски	по системе краски			м²	527		площадь окраски стен, акцентов и потолков; 1 слой перед окраской; расход — по ТУ грунтовки

					Проект: Дом 120 м²
	Лист	№ док.	Подпись	Дата	Спецификация отделочных материалов
Дизайнер	Кырлан А.С.			19.10.26	

Стадия	Лист	Листов
П	С2	128


1 Порог 15 мм: мокрая зона — жилое помещение (М 1:5)

Применение: двери Д-3, Д-8

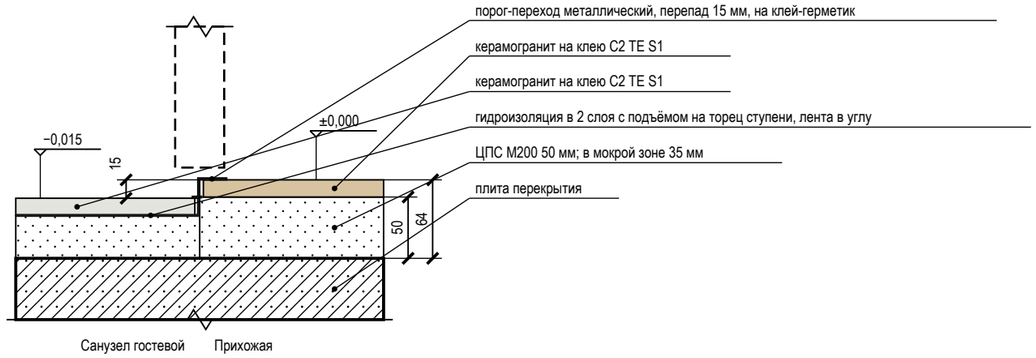


2 Дверь скрытого монтажа в плоскости стены, плинтус (М 1:5)

Применение: двери Д-1, Д-2, Д-3, Д-4, Д-5, Д-6, Д-7, Д-10, Д-9, Д-8

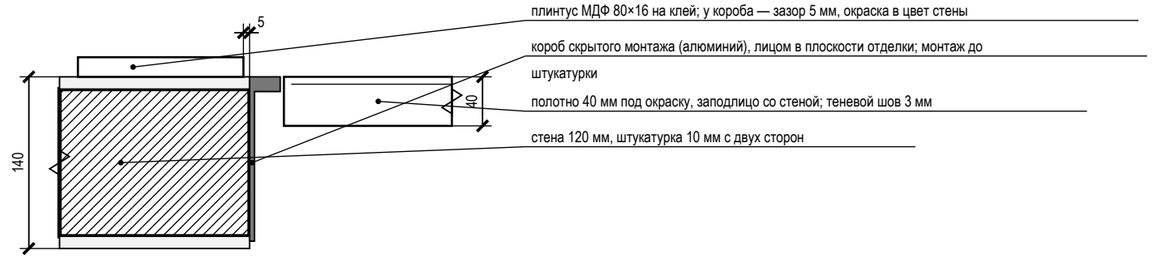


3 Короб стояков К1-1 с люком и звукоизоляцией (М 1:10)

Применение: пом. 4, 1

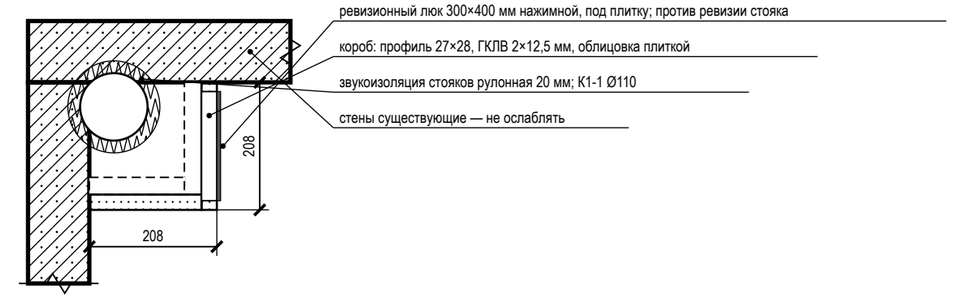


4 Гидроизоляция санузла: заход на стены 200 мм, примыкание ванны (М 1:20)

Применение: пом. 4, 13

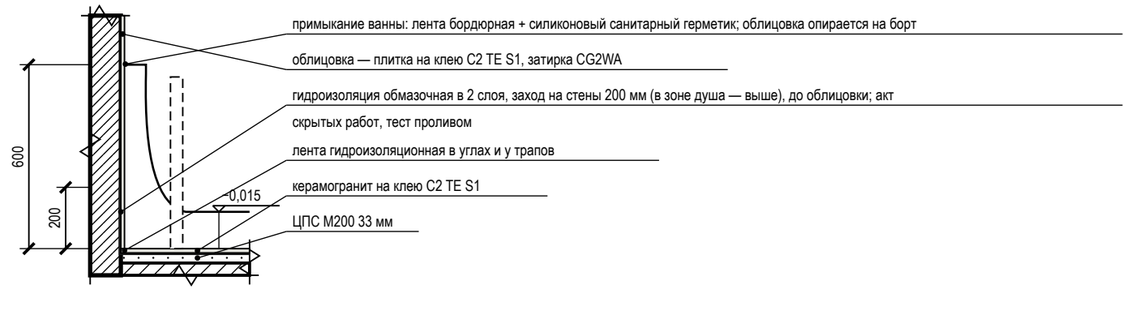

5 Плинтус МДФ 80×16 мм у окрашенной стены (М 1:10)

Применение: пом. 1, 2, 3, 5, 6, 7, 8, 9, 10, 11, 12

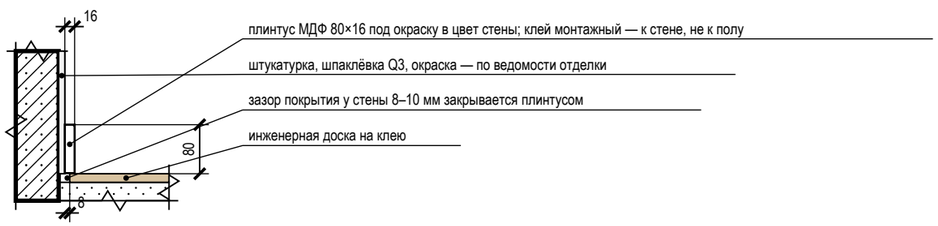

Условные обозначения

- железобетон (плита, стены)
- кладка, перегородка
- стяжка, раствор
- гипсокартон ГКЛВ
- звукоизоляция, эластичный заполнитель
- плитка, керамогранит на клею
- инженерная доска (покрытие пола)
- металлический профиль (порог, Т-профиль, короб двери)
- гидроизоляция (обмазочная, лента)

Примечания

1. Узлы — типовые решения проекта для мест, отмеченных выносками на листе схемы расположения развёрток и узлов; размеры — в мм, отметки — в м от ±0,000.
2. Узлы с гидроизоляцией, закладными и коробами скрытого монтажа принимаются по актам скрытых работ до закрытия отделкой; гидроизоляция — после теста проливом (24 ч).
3. Марки изделий (порог, Т-профиль, короб скрытой двери, люк) — по спецификациям; замена — на аналог с теми же габаритами по согласованию с автором проекта.

					Проект: Дом 120 м²
	Лист	№ док.	Подпись	Дата	
Дизайнер	Кырлан А.С.			19.10.26	Узлы

Стадия	Лист	Листов
П	С3	128

выпуск 19.10.2026 № 66b2a77b4d · стр. 128 из 128