ДИЗАЙН-ПРОЕКТ ИНТЕРЬЕРА

Квартира 65 м²

Скандинавский

65,24 м²

светло · спокойно · уютно (hygge) · естественно · функционально · в меру (lagom)

Палитра из: тёплые нейтрали NCS (стены по ведомости — S 1002-Y50R / S 1502-Y50R близки к ним), акцент — пыльный синий в текстиле.

ПАЛИТРА 60 / 30 / 10

NCS S 0500-N	NCS S 1500-N	NCS S 2002-Y	NCS S 4010-R90B
60 %	30 %	30 %	10 %



Визуализация 1 · Вид сверху (3D): планировка с мебелью, текстилем и декором

ОБЪЕКТ	ОБЩАЯ ПЛОЩАДЬ	ПОМЕЩЕНИЙ
Квартира 65 м²	65,24 м²	9, из них жилых 3
СТИЛЬ	**СТАДИЯ**	**ШИФР**
Скандинавский	Рабочий проект	ГД-2026-007-АИ

КАК ОСТАВИТЬ ПРАВКУ

Нажмите кнопку «Правка к этому листу» в правом верхнем углу любого листа — лист откроется на сайте студии: отметьте место на чертеже и наговорите замечание голосом или напишите текстом.

Или откройте все листы проекта:

alex1986-rgb.github.io/linea-design-studio/review.html?p=gost-kv65

АВТОР ПРОЕКТА

Кырлан Александр Сергеевич

Октябрь 2026

					Проект: Квартира 65 м²
	Лист	№ док.	Подпись	Дата	Титульный лист
Дизайнер	Кырлан А.С.			21.10.26	

Стадия	Лист	Листов
П	1	80

выпуск 09.10.2026 № da691793fd · стр. 1 из 80

Правка к этому листу

Список листов

Лист	Наименование
1	Титульный лист
2	Список листов
3	План планировки от заказчика
4	План монтажный
5	Кухня (пом. 3). Монтажная схема
6	Шкафы. Монтажная схема
7	Карта покрытий стен
8	Колерная карта
9	План размещения мебели и оборудования
10	Спецификация мебели и оборудования
11	Спецификация мебели и оборудования (продолжение)
12	Ведомости изделий, техники и фурнитуры
13	План выводов сантехники
14	Схема разводки водопровода и канализации
15	Спецификация сантехнического оборудования
16	План размещения дверей
17	План потолков
18	План розеток и электровыводов
19	План слаботочных сетей
20	План освещения
21	Спецификация светильников и сценарии освещения
22	Управление светильниками
23	План вентиляции
24	План отопления
25	План покрытий пола
26	Раскладка плитки. Планы полов
27	Раскладка плитки. Прихожая. Коридор. Санузел. Ванная
28	Визуализация. Вид сверху
29	Визуализация гардеробной
30	Развёртки стен А, Б. Гардеробная (пом. 1)
31	Развёртка стены Г. Гардеробная (пом. 1)
32	Визуализация спальни
33	Визуализация спальни
34	Развёртка стены А. Спальня (пом. 2)
35	Развёртка стены Б. Спальня (пом. 2)
36	Развёртка стены В. Спальня (пом. 2)
37	Развёртка стены Г. Спальня (пом. 2)
38	Визуализация кухни-гостиной
39	Визуализация кухни-гостиной
40	Визуализация кухни-гостиной

Лист	Наименование
41	Визуализация кухни-гостиной
42	Развёртка стены В2. Кухня-гостиная (пом. 3), кухонный фронт
43	Развёртка стены Г. Кухня-гостиная (пом. 3), кухонный фронт
44	Развёртка стены А1. Кухня-гостиная (пом. 3)
45	Развёртки стен А2, Б1. Кухня-гостиная (пом. 3)
46	Развёртки стен Б2, Б3, В1. Кухня-гостиная (пом. 3)
47	Визуализация прихожей
48	Визуализация прихожей
49	Развёртки стен. Прихожая (пом. 4)
50	Визуализация коридора
51	Визуализация коридора
52	Развёртка стены А. Коридор (пом. 5)
53	Развёртки стен Б, Г. Коридор (пом. 5)
54	Развёртка стены В. Коридор (пом. 5)
55	Визуализация санузла
56	Развёртки стен А, Б, В. Санузел (пом. 6)
57	Развёртка стены Г. Санузел (пом. 6)
58	Визуализация ванной
59	Визуализация ванной
60	Развёртки стен А, Б. Ванная (пом. 7)
61	Развёртки стен В, Г. Ванная (пом. 7)
62	Визуализация кладовой
63	Развёртки стен А, Б. Кладовая (пом. 8)
64	Развёртка стены В. Кладовая (пом. 8)
65	Визуализация детской
66	Визуализация детской
67	Визуализация детской
68	Визуализация детской
69	Развёртка стены А. Детская (пом. 9)
70	Развёртка стены Б. Детская (пом. 9)
71	Развёртка стены В. Детская (пом. 9)
72	Развёртка стены Г. Детская (пом. 9)
Д_1	Система хранения М_01
Д_2	Шкаф-купе М_15
Д_3	Система хранения М_16
Д_4	Шкаф распашной М_17
Д_5	Кухня (пом. 3). Развёртка гарнитура
С1	Ведомость отделки помещений
С2	Спецификация отделочных материалов
С3	Узлы

Общие указания

1. Размеры даны в мм от чистовых поверхностей стен: слой штукатурки 20 мм по блоку и 5 мм шпаклёвки по ГКЛ учтён. Перед заказом встроенной мебели — контрольный обмер после штукатурки.
2. Привязки мебели — от стен и углов помещения, а не от другой мебели.
3. Розетки, выводы и выключатели под мебель — см. лист 18 «План розеток и электровыводов»; сантехприборы и выводы воды — лист 13.
4. План расстановки не является документацией для изготовления мебели: изделия — по чертежам мебельщика; покупную мебель заменять только на изделия не больше габарита из спецификации (лист 10).
5. Встроенная мебель «стена в стену» — с зазором 10 мм с каждой стороны или с компенсаторами.
6. Развёртки — вид на стену изнутри помещения, по часовой стрелке; расположение стен на схеме листа развёртки; размеры — в мм по чистовым поверхностям; отметки — в м от ±0,000; высоты Н — от чистого пола помещения до оси изделия, у декора — до центра.
7. Красные цепочки — привязки электроточек и выводов: по горизонтали от угла чистовых стен, по вертикали от чистого пола, до оси изделия; звенья короче 3 мм на листе вынесены во второй ярус (ближняя к стене цепочка).
8. У знака электроточки: марка (Р — розетка, S — выключатель, Св — светильник, ЭВ вывод кабеля), ×N — число постов в рамке, гр. — группа щита, Н — высота оси от чистого пола, мм; группы по клавишам выключателя — на листе выключателей.
9. Схема мебели, приборов и декора не является технической документацией для производства мебели; габариты — по паспортам изделий.
10. Марки позиций: М_NN — мебель, ОБ_NN — оборудование, С_NN — сантехника; О-N отделка (ведомость отделочных материалов, серия С).
11. Размеры мебели и изделий на заказ уточнить по месту после отделочных работ.

	Лист	№ док.	Подпись	Дата	
Дизайнер	Кирлан А.О.			21.10.26	

Проект: Квартира 65 м²

Список листов

Стадия	Лист	Листов
П	2	80

выпуск 09.10.2026 № da691793fd · стр. 2 из 80

Правка к этому листу

Отметки по высоте

±0,000	чистый пол пом. 1–5, 8, 9; отсчёт высот
−0,015	чистый пол пом. 6, 7, ниже на 15 мм
−0,064	верх плиты — расчёт, не замер (задание на обмер)
сущ. пол	снимается до плиты; не замерен (задание на обмер)

Примечания


1. Размеры — в мм по чистым поверхностям стен до отделки (по плану заказчика); площади — в м² по тем же размерам. До начала работ выполнить контрольный обмер.
2. Источник плана: растровый скан плана заказчика, размеры сняты с размерных цепочек, на объекте не замерены.
3. За отметку ±0,000 принят чистый пол, не существующий (блок отметок). Н пот. — высота от чистого пола до плиты перекрытия.
4. Толщины стен: наружные 300 мм, перегородки 120 мм; отличающиеся толщины и уступы размерами на плане.
5. Несущие стены не определены: до технического заключения все стены считать несущими; проёмы и штробы в них не выполнять.
6. Дверные проёмы показаны без заполнения (двери — лист 16); высота дверных проёмов 2100 мм, проёмов без двери 2100 мм; низ окон (подоконник) 800 мм от чистого пола, высота окон 1600 мм.
7. Диагонали — контрольные размеры; расхождение более 5 мм подписать на плане как перекос.
8. Размеры проверить на месте до начала работ; расхождение контрольных промеров ≤ 2 %.
9. Размеры короче 1 мм на листе цепочкой не показаны (две выносные линии на таком расстоянии сливаются): пом. 5, стена В — 40 мм от угла до проёма.

Экспликация помещений

№	Наименование	Площадь, м²
1	Гардеробная	4,20
2	Спальня	8,27
3	Кухня-гостиная	18,91
4	Прихожая	4,15
5	Коридор	5,51
6	Санузел	1,83
7	Ванная	3,85
8	Кладовая	2,50
9	Детская	16,02
	Итого (общая площадь)	**65,24**

Условные обозначения


- существующие стены (сечение)
- окно (рама, остекление)
- проём существующий, без заполнения (откосы)
- стояк: К1 — канализация, В1 — ХВС, Т3 — ГВС
- проектная конструкция — на объекте её нет (контур)
- диагональ помещения — контроль прямоугольности
- (1) номер помещения, площадь м²

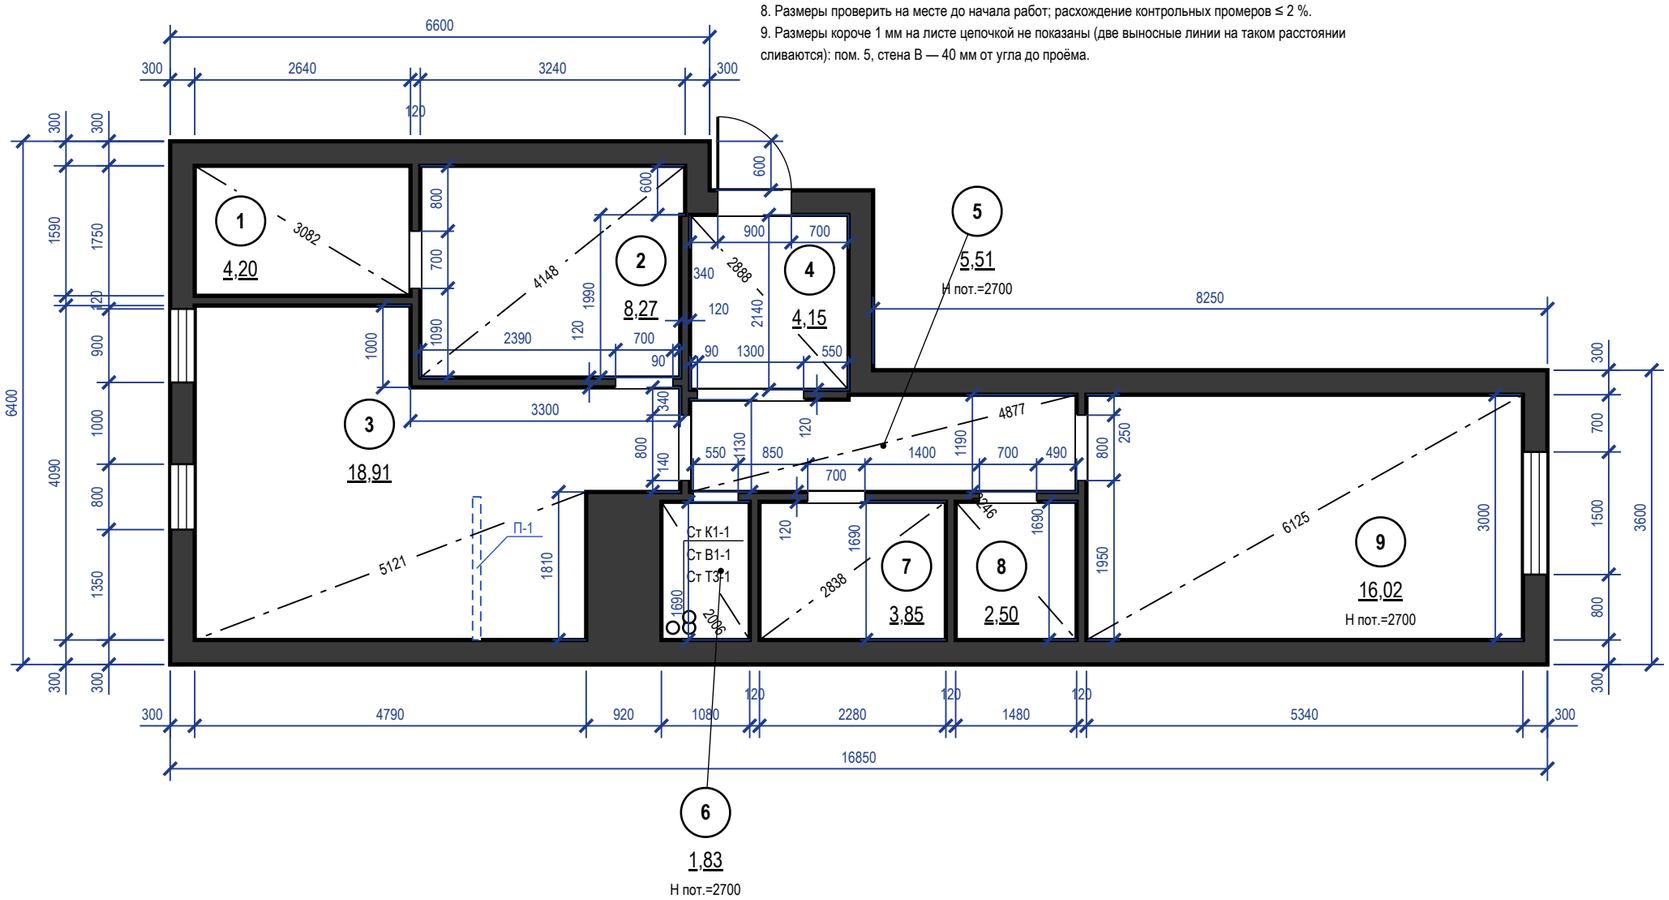

					Проект: Квартира 65 м²	
	Лист	№ док.	Подпись	Дата	План планировки от заказчика	Стадия / Лист / Листов
Дизайнер	Кырлан А.С.			21.10.26		П / 3 / 80

выпуск 09.10.2026 № da691793fd · стр. 3 из 80

Правка к этому листу

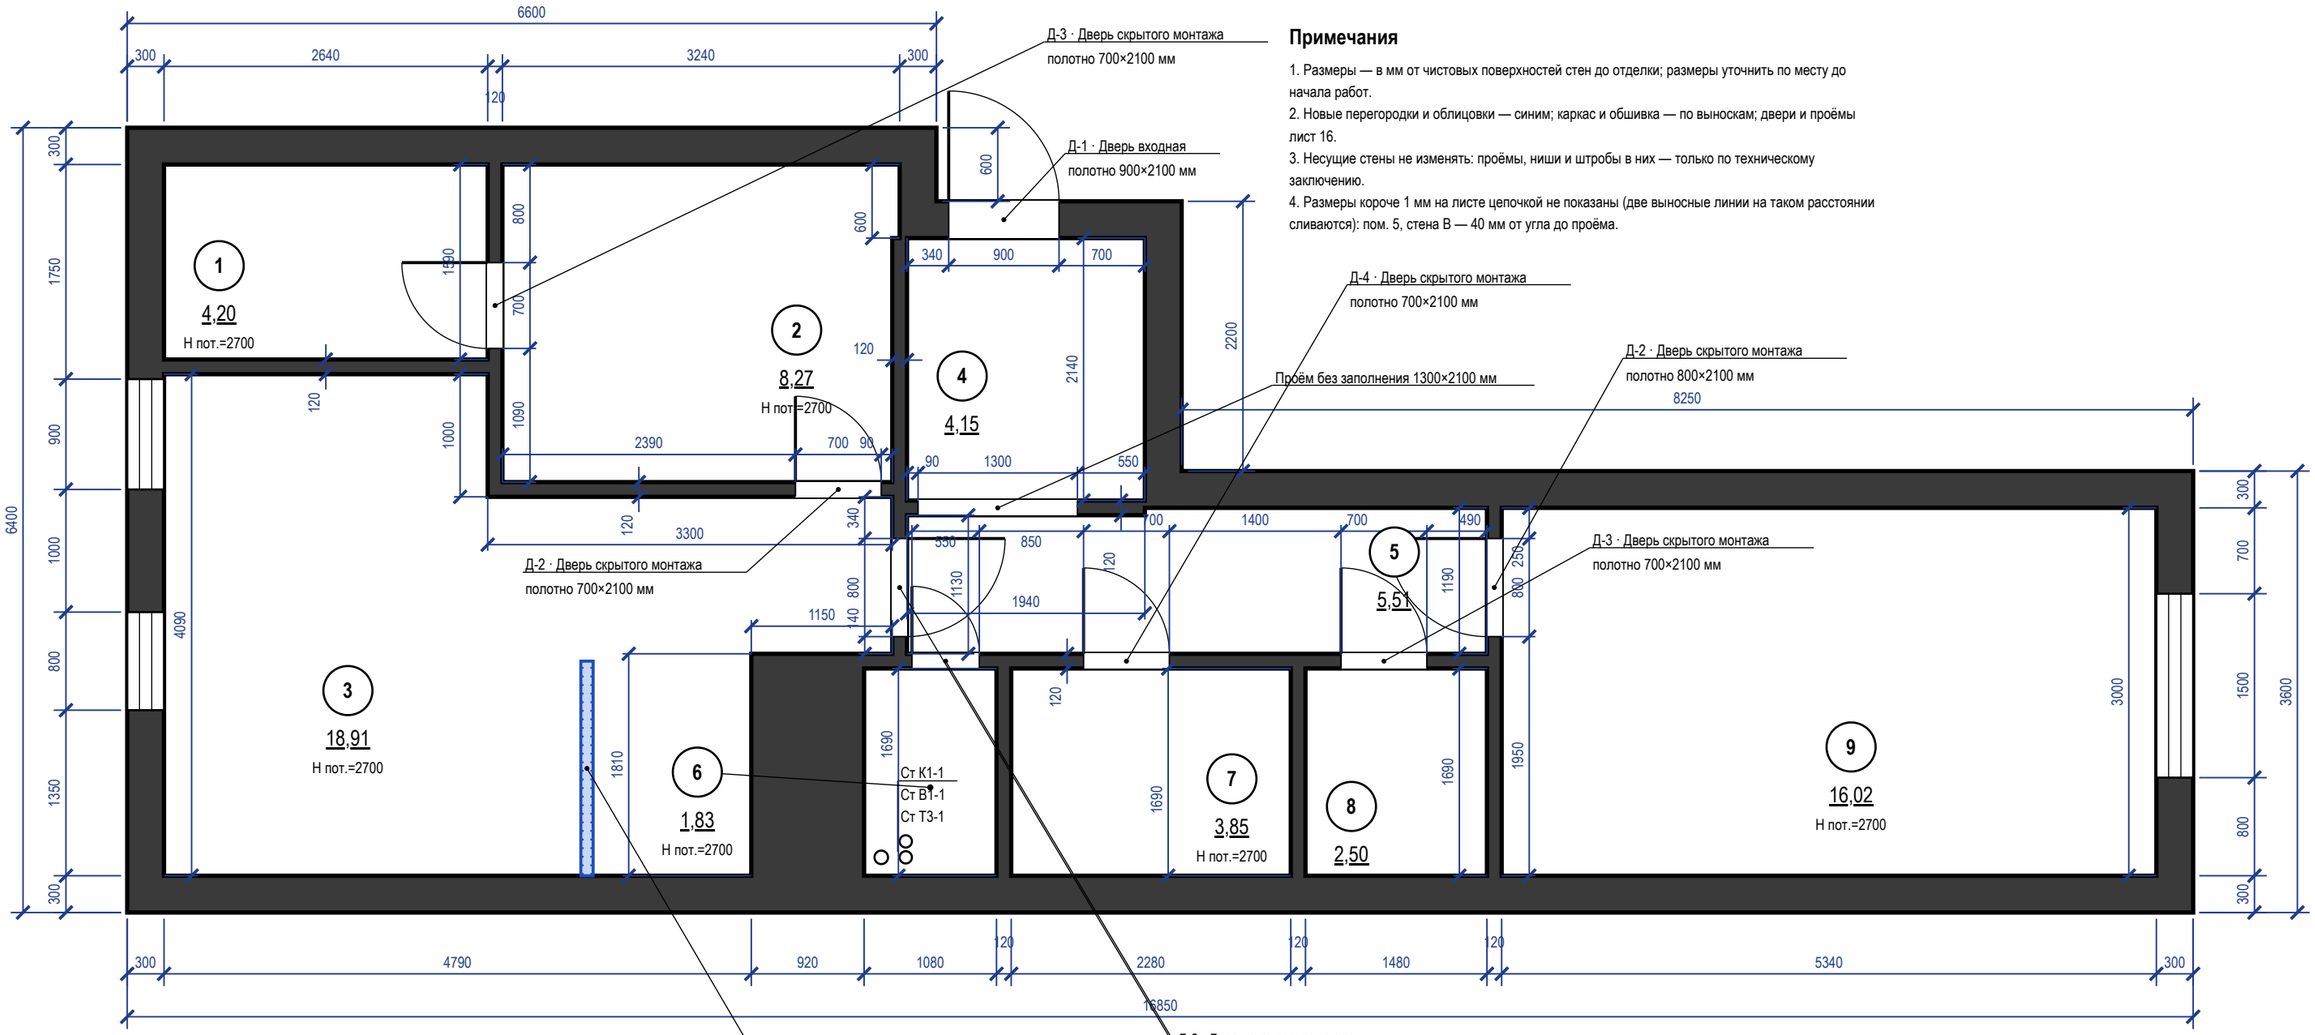

Примечания

1. Размеры — в мм от чистовых поверхностей стен до отделки; размеры уточнить по месту до начала работ.
2. Новые перегородки и облицовки — синим; каркас и обшивка — по выноскам; двери и проёмы лист 16.
3. Несущие стены не изменять: проёмы, ниши и штробы в них — только по техническому заключению.
4. Размеры короче 1 мм на листе цепочкой не показаны (две выносные линии на таком расстоянии сливаются): пом. 5, стена В — 40 мм от угла до проёма.

Экспликация помещений

№	Наименование	Площадь, м²
1	Гардеробная	4,20
2	Спальня	8,27
3	Кухня-гостиная	18,91
4	Прихожая	4,15
5	Коридор	5,51
6	Санузел	1,83
7	Ванная	3,85
8	Кладовая	2,50
9	Детская	16,02
	Итого (общая площадь)	**65,24**

	Лист	№ док.	Подпись	Дата
Дизайнер	Кырлан А.С.			21.10.26

Проект: Квартира 65 м²


План монтажный

Стадия	Лист	Листов
П	4	80


выпуск 09.10.2026 № da691793fd · стр. 4 из 80

Правка к этому листу

Привязка выводов и крепление модулей

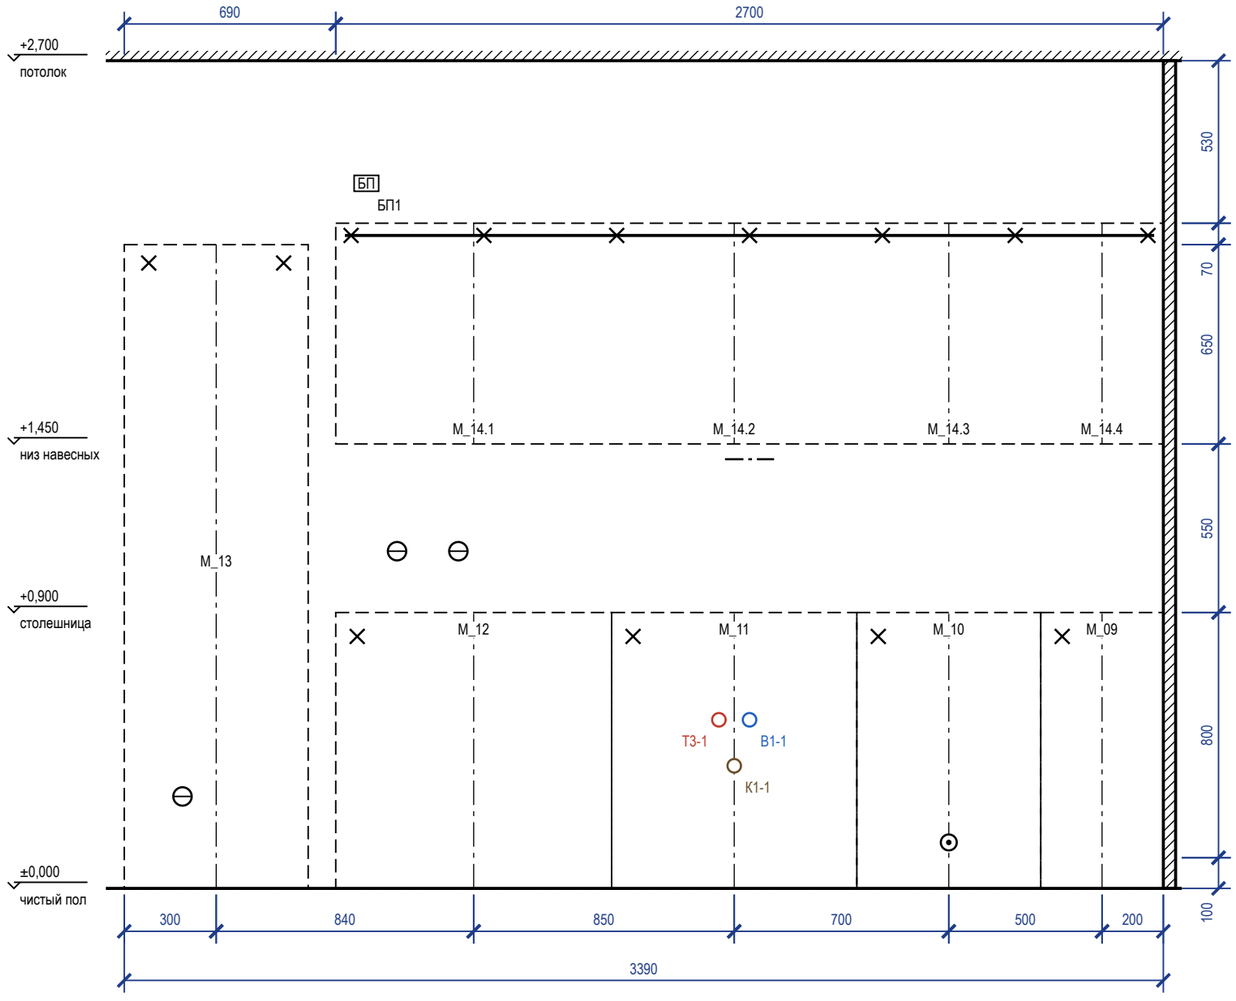

План столешницы

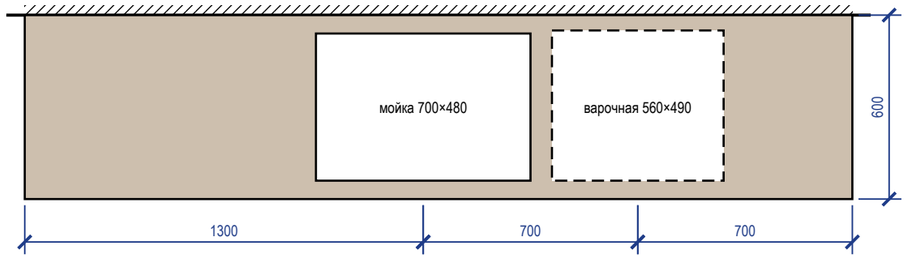

Привязка выводов к осям модулей

Код	Назначение	Модуль	От оси, мм	H, мм	Размещение
	розетка — холодильник	M_13	−110	300	за пеналом
БП1	блок питания	M_14.1	−350	2300	в навесном модуле
	розетка — рабочая зона	M_12	−250	1100	над столешницей (фартук)
	розетка ×2 — рабочая зона	M_12	−50	1100	над столешницей (фартук)
T3-1	T3 — межос. 100	M_11	−50	550	в модуле мойки
K1-1	K1 Ø50 — мойка	M_11	0	400	в модуле мойки
	светодиодная лента — подсветка столешницы	M_11	+50	1400	в профиле по низу навесного модуля
B1-1	B1 — межос. 100	M_11	+50	550	в модуле мойки
	вывод кабеля — варочная панель	M_10	0	150	в соседнем модуле, за ящиком

Зазоры под отделку

Поверхность	Отделка	Зазор, мм	Учесть
фартук	плитка / стеновая панель	10	от чернового основания до корпуса навесных и столешницы
стены	окраска	5	под штукатурку и шпаклёвку за пеналом
пол	инженерная доска		цоколь — после укладки пола, опоры ±20 мм

Условные обозначения

- навесной модуль (невидимый контур)
- ось модуля (от неё — привязка вывода)
- анкер / уголок крепления к стене
- розетка на стене
- вывод кабеля к технике
- B1 — вывод воды B1 / T3, канализации K1

Примечания

1. Выводы — по проекту электрики и ВК; привязка по горизонтали — от оси модуля (плюс — вправо по виду), по высоте — от чистого пола до оси вывода.
2. Пенал — уголки к стене 2 шт. сверху; нижние модули — стяжками между собой и уголком к стене; ряд выставить по уровню опорами цоколя.
3. Розетки над столешницей — не ниже 150 мм над ней и не за корпусом техники; розетка за ПММ, духовым шкафом и холодильником — только в соседнем модуле или в зоне цоколя с доступом.
4. Столешница — вырезы по шаблонам выбранных моделей мойки и варочной панели; торцы у стены — герметик, пристеночный плинтус.


					Проект: Квартира 65 м²
	Лист	№ док.	Подпись	Дата	Кухня (пом. 3). Монтажная схема
Дизайнер	Кырлан А.С.			21.10.26	

Стадия	Лист	Листов
П	5	80


выпуск 09.10.2026 № da691793fd · стр. 5 из 80

Правка к этому листу


Система хранения M_01 (пом. 1)

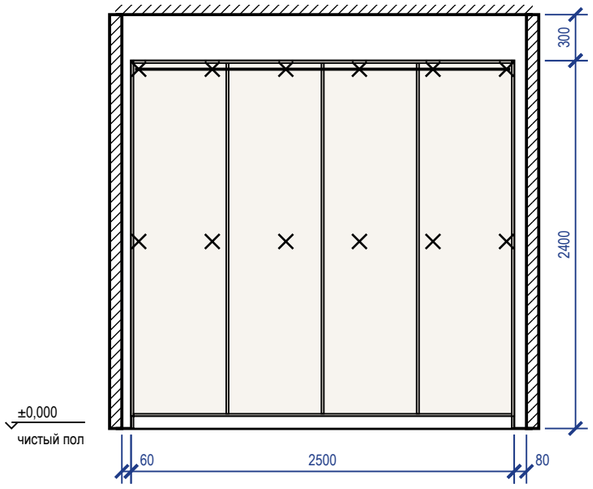


Шкаф-купе M_15 (пом. 4)

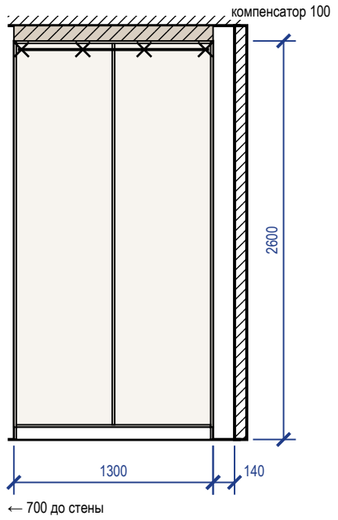

Система хранения M_16 (пом. 8)

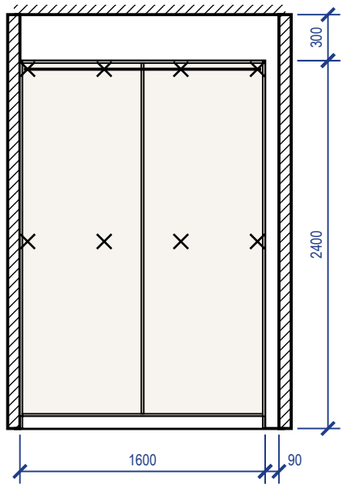

Шкаф распашной M_17 (пом. 9)

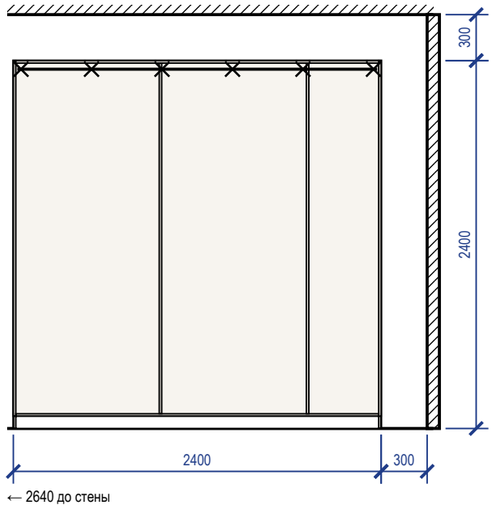

Крепление и зазоры под отделку

Марка	Помещение, стена	Основание	Отделка стены	Зазор, мм	Крепёж по планке	От опрокидывания
M_01	Гардеробная (1), стена А	по основанию — см. таблицу крепежа	окраска	5	анкер 12 шт. (2 ряда)	крепление к стене, 3 точки
M_15	Прихожая (4), стена Б	по основанию — см. таблицу крепежа	окраска	5	анкер 4 шт., шаг 400	уголки 2 шт.
M_16	Кладовая (8), стена Б	по основанию — см. таблицу крепежа	окраска	5	анкер 8 шт. (2 ряда)	уголки 2 шт.
M_17	Детская (9), стена А	по основанию — см. таблицу крепежа	окраска	5	анкер 6 шт., шаг 460	уголки 2 шт.

Крепёж по основанию стены

Основание стены	Крепёж
бетон, ж/б	анкер-шуруп 7,5×72 или дюбель 8×60 с шурупом 5×70
кирпич полнотелый	дюбель 8×80 с шурупом 5×90
газобетон, пазогребень	дюбель для газобетона 10×100 или химический анкер
гипсокартон	закладная до обшивки (брус 40×80 или фанера 18 мм), саморез в закладную

Условные обозначения

- анкер / уголок крепления к стене
- корпус и полки ЛДСП (вид на стену)
- компенсатор — короб до потолка

Примечания


1. Установочные размеры — от чистого пола и чистых стен; перед установкой контрольный замер после отделки.
2. Порядок: корпус выставить по уровню опорами цоколя → закрепить к стене по задней планке → навесить двери и фасады, отрегулировать зазоры → подогнать и закрепить компенсатор.
3. Анкеры — с шагом не более 500 мм, не ближе 50 мм от края планки; на ГКЛ только в закладную, установленную до обшивки.
4. Скрытые коммуникации под анкеры проверить детектором; трассы электрики по плану розеток.

	Лист	№ док.	Подпись	Дата
Дизайнер	Кырлан А.С.			21.10.26

Проект: Квартира 65 м²

Шкафы. Монтажная схема	Стадия	Лист	Листов
	П	6	80

Правка к этому листу

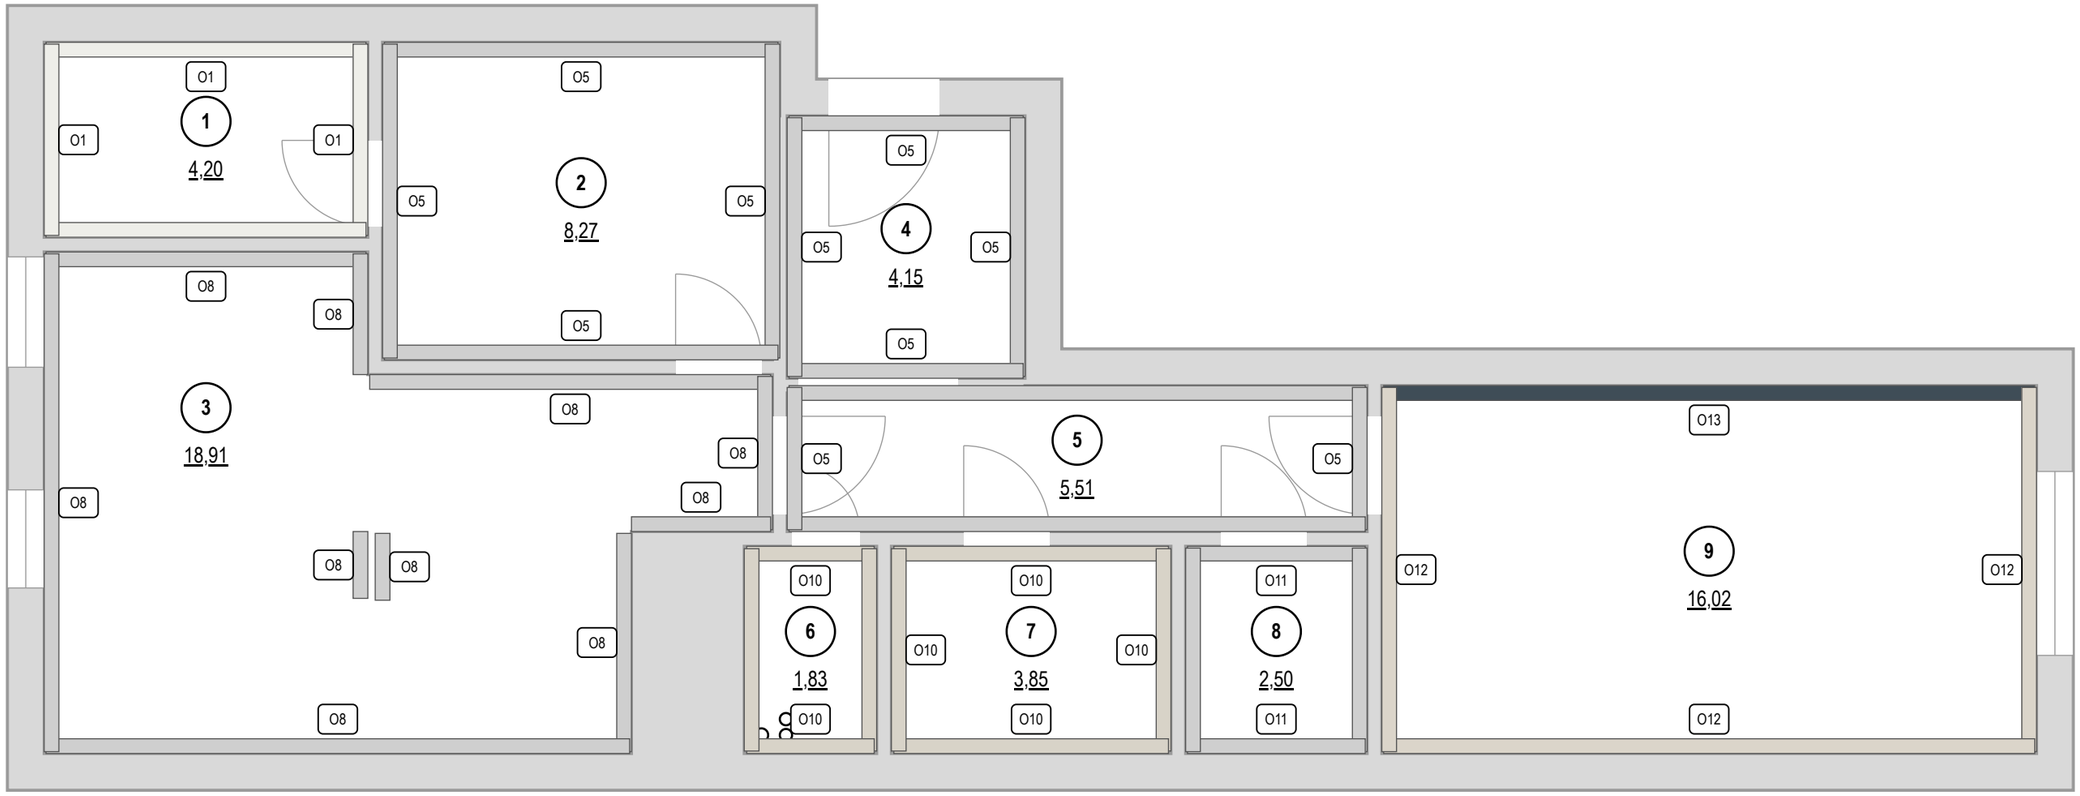

Покрытия стен

Марка	Покрытие	Помещение: S, м²	Итого, м²
O1	окраска Tikkurila · V503 «Winter»	1: 21,0	21,0
O5	окраска Tikkurila · S 1502-Y50R	2: 28,2; 4: 17,1; 5: 21,5	66,8
O8	окраска Tikkurila · S 1002-Y50R	3: 50,7	50,7
O10	облицовка плиткой Italon · 610010001195 «Charme Extra» 600×1200 мм	6: 13,5; 7: 19,7	33,1
O11	окраска Tikkurila · S 0502-Y	8: 15,3	15,3
O12	окраска Farrow & Ball · No. 241 «Skimming Stone»	9: 26,3	26,3
O13	окраска Farrow & Ball · No. 30 «Hague Blue»	9: 14,3	14,3

Площади — нетто, по развёрткам (за вычетом проёмов и фартука); высоты помещений — от чистого пола.

					Проект: Квартира 65 м²
	Лист	№ док.	Подпись	Дата	Карта покрытий стен
Дизайнер	Кырлан А.С.			21.10.26	

Стадия	Лист	Листов
П	7	80

выпуск 09.10.2026 № da691793fd · стр. 7 из 80

Правка к этому листу

Колерная карта по помещениям

Помещение	Поверхность	Образец	Поз.	Система и код цвета	Производитель, линейка / материал, артикул	Блеск	Класс EN 13300	LRV	Площадь
1. Гардеробная 4,2 м²	стены		**K1**	Tikkurila V503	Tikkurila · Harmony	матовая	1	86	21,4 м²
	потолок		**K2**	Tikkurila V503	Tikkurila · Anti-Reflex 2	глубокомат.	2	86	4,2 м²
	пол		**KM1**	по образцу	Quick-Step · Impressive				4,2 м²
	плинтус		**K3**	Tikkurila V503	Orac Decor · Contour (Luxxus)			86	7,8 м
2. Спальня 8,27 м²	стены		**K4**	NCS S 1502-Y50R	Tikkurila	глубокомат.	2	72	28,5 м²
	потолок		**K5**	NCS S 0300-N	Tikkurila	глубокомат.	2	92	8,3 м²
	пол		**KM1**	по образцу	Quick-Step · Impressive				8,3 м²
	плинтус		**K6**	NCS S 0300-N	Orac Decor · Contour (Luxxus)	полуматов.		92	10,3 м
3. Кухня-гостиная 18,91 м²	стены		**K7**	NCS S 1002-Y50R	Tikkurila	полуматов.	1	82	48,3 м²
	потолок		**K8**	NCS S 0300-N	Tikkurila	глубокомат.	1	92	18,9 м²
	пол		**KM1**	по образцу	Quick-Step · Impressive				18,9 м²
	плинтус		**K6**	NCS S 0300-N	Orac Decor · Contour (Luxxus)	полуматов.		92	18,6 м
4. Прихожая 4,15 м²	стены		**K9**	NCS S 1502-Y50R	Tikkurila	полуматов.	1	72	17,4 м²
	потолок		**K8**	NCS S 0300-N	Tikkurila	глубокомат.	1	92	4,2 м²
	пол		**K10**	Kerama Marazzi SG501600R	Kerama Marazzi · Королевская дорога				4,2 м²
	плинтус		**K6**	NCS S 0300-N	Orac Decor · Contour (Luxxus)	полуматов.		92	6,0 м
5. Коридор 5,51 м²	стены		**K9**	NCS S 1502-Y50R	Tikkurila	полуматов.	1	72	21,8 м²
	потолок		**K8**	NCS S 0300-N	Tikkurila	глубокомат.	1	92	5,5 м²
	пол		**K10**	Kerama Marazzi SG501600R	Kerama Marazzi · Королевская дорога				5,5 м²
	плинтус		**K6**	NCS S 0300-N	Orac Decor · Contour (Luxxus)	полуматов.		92	7,0 м
6. Санузел 1,83 м²	стены		**K11**	Italon 610010001195	Italon · Charme Extra				13,9 м²
	потолок		**K8**	NCS S 0300-N	Tikkurila	глубокомат.	1	92	1,8 м²
	пол		**K10**	Kerama Marazzi SG501600R	Kerama Marazzi · Королевская дорога				1,8 м²
7. Ванная 3,85 м²	стены		**K11**	Italon 610010001195	Italon · Charme Extra				20,1 м²
	потолок		**K8**	NCS S 0300-N	Tikkurila	глубокомат.	1	92	3,9 м²
	пол		**K10**	Kerama Marazzi SG501600R	Kerama Marazzi · Королевская дорога				3,9 м²
8. Кладовая 2,5 м²	стены		**K12**	NCS S 0502-Y	Tikkurila	матовая	2	86	15,6 м²
	потолок		**K5**	NCS S 0300-N	Tikkurila	глубокомат.	2	92	2,5 м²
	пол		**KM1**	по образцу	Quick-Step · Impressive				2,5 м²
	плинтус		**K6**	NCS S 0300-N	Orac Decor · Contour (Luxxus)	полуматов.		92	5,6 м
9. Детская 16,02 м²	стены		**K13**	Farrow & Ball No. 241	Farrow & Ball · Modern Emulsion	матовая	1	67	26,5 м²
	акцент А		**K14**	Farrow & Ball No. 30	Farrow & Ball · Modern Emulsion	матовая	1	7	14,4 м²
	потолок		**K2**	Tikkurila V503	Tikkurila · Anti-Reflex 2	глубокомат.	2	86	16,0 м²
	пол		**KM1**	по образцу	Quick-Step · Impressive				16,0 м²
	плинтус		**K15**	Farrow & Ball No. 241	Orac Decor · Contour (Luxxus)			67	15,9 м

Примечания

1. Цвет утверждается только по выкрасу на объекте: формат от А3 до 1000×1000 мм на загрунтованном ГКЛ, в 2 слоя (как на стене), не на белой шпаклёвке; смотреть днём и при свете проекта своего помещения, рядом с образцами пола и фасадов. Подпись на обороте: код, бренд и веер, дата.
2. Колеровка машинная в колеровочном центре бренда; каждый код — за один проход, одной партией на весь объём. Колеровщику передаётся только система и код утверждённого веера; плашки и HEX на листе — ориентир, печать не является эталоном цвета.
3. Класс мокрого истирания — EN 13300 (ISO 11998); блеск — по ГОСТ 31975 (ISO 2813), геометрия 60°. LRV — пересчёт координаты L каталога производителя (Y = ((L*+16)/116)³); «≈» — расчёт по HEX, справочно.
4. Площади поверхностей — тем же способом и с теми же цифрами, что в ведомости отделки (способ счёта — в общих указаниях); объём краски к заказу, фасовка и материалы КМ — в спецификации отделочных материалов.
5. Перечень выкрасов составлен по кодам колерной карты; к основному тону стен добавить на выкрас 2 соседних тона того же веера (светлее и темнее), статус отмечать в графе «Статус» при согласовании.
6. Узор штриховки сегмента «без кода цвета» на полосах 60/30/10 прерывается под числами долей (белая подложка), границы сегментов не прерываются.

Схема палитры проекта


Стиль: Скандинавский · схема: нейтральная

основной	второстепенный	второстепенный	акцентный
NCS S 0500-N	**NCS S 1500-N**	**NCS S 2002-Y**	**NCS S 4010-R90B**
нейтральный белый LRV 85 в отделке не применён	светлый нейтральный серый LRV 64 в отделке не применён	серый камень, тёплый LRV 55 в отделке не применён	пыльный синий LRV 27 в отделке не применён

План 60/30/10



Окраска, факт — по площади стен, акцентов, потолков

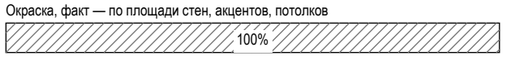

окрашено всего 293,2 м²; второстепенный тон несут мебель и текстиль

Текстиль и декор в цветах вне палитры проекта

- Tikkurila H487 Pumice — пом. 9 (T7)
- Tikkurila V503 Winter — пом. 9 (T8)
- Tikkurila V484 Driftwood — пом. 9 (T9)
- Farrow & Ball No. 229 Elephant's Breath — пом. 9 (T10)
- Farrow & Ball No. 47 Green Smoke — пом. 9 (T11)
- Farrow & Ball No. 30 Hague Blue — пом. 9 (T12)

Условные обозначения

- **K1** Tikkurila V503 · Winter · Harmony · матовая · кл. 1
- **K2** Tikkurila V503 · Winter · Anti-Reflex 2 · глубокомат. · кл. 2
- **K3** Tikkurila V503 · Winter · Contour (Luxxus)
- **K4** NCS S 1502-Y50R · Tikkurila · глубокомат. · кл. 2
- **K5** NCS S 0300-N · Tikkurila · глубокомат. · кл. 2
- **K6** NCS S 0300-N · Orac Decor Contour (Luxxus) · полуматов.
- **K7** NCS S 1002-Y50R · Tikkurila · полуматов. · кл. 1
- **K8** NCS S 0300-N · Tikkurila · глубокомат. · кл. 1
- **K9** NCS S 1502-Y50R · Tikkurila · полуматов. · кл. 1
- **K10** Kerama Marazzi SG501600R · Королевская дорога · Королевская дорога
- **K11** Italon 610010001195 · Charme Extra · Charme Extra
- **K12** NCS S 0502-Y · Tikkurila · матовая · кл. 2
- **K13** Farrow & Ball No. 241 · Skimming Stone · Modern Emulsion · матовая · кл. 1
- **K14** Farrow & Ball No. 30 · Hague Blue · Modern Emulsion · матовая · кл. 1
- **K15** Farrow & Ball No. 241 · Skimming Stone · Contour (Luxxus)
- **KM1** инженерная доска · IM1848

дерево (доска, паркет, ламинат) — рисунок досок

HEX не задан — цвет только по коду и вееру

К — позиция окраски (код + продукт + блеск), КМ — позиция материала, тон КМ — по описанию артикула, эталон — образец материала; ≈ LRV — расчёт по HEX, справочно

Перечень выкрасов на согласование

№	Код	Бренд / веер	Пом. / стена	Подложка	Формат	Статус
1	V503	Tikkurila	1, 9	ГКЛ, загрунтованный под эту краску; МДФ, загрунтованный под эмаль	600×1000; 300×600	к выполнению
2	S 1502-Y50R	NCS Tikkurila	2, 4, 5	ГКЛ, загрунтованный под эту краску	600×1000	к выполнению
3	S 0300-N	NCS Tikkurila	2, 3, 4, 5, 6, 7, 8	ГКЛ, загрунтованный под эту краску; МДФ, загрунтованный под эмаль	600×1000; 300×600	к выполнению
4	S 1002-Y50R	NCS Tikkurila	3	ГКЛ, загрунтованный под эту краску	600×1000	к выполнению

… ещё 3 выкрасов — в ведомости отделки


	Лист	№ док.	Подпись	Дата
Дизайнер	Кырлан А.С.			21.10.26

Проект: Квартира 65 м²

Колерная карта

Стадия	Лист	Листов
П	8	80

Правка к этому листу

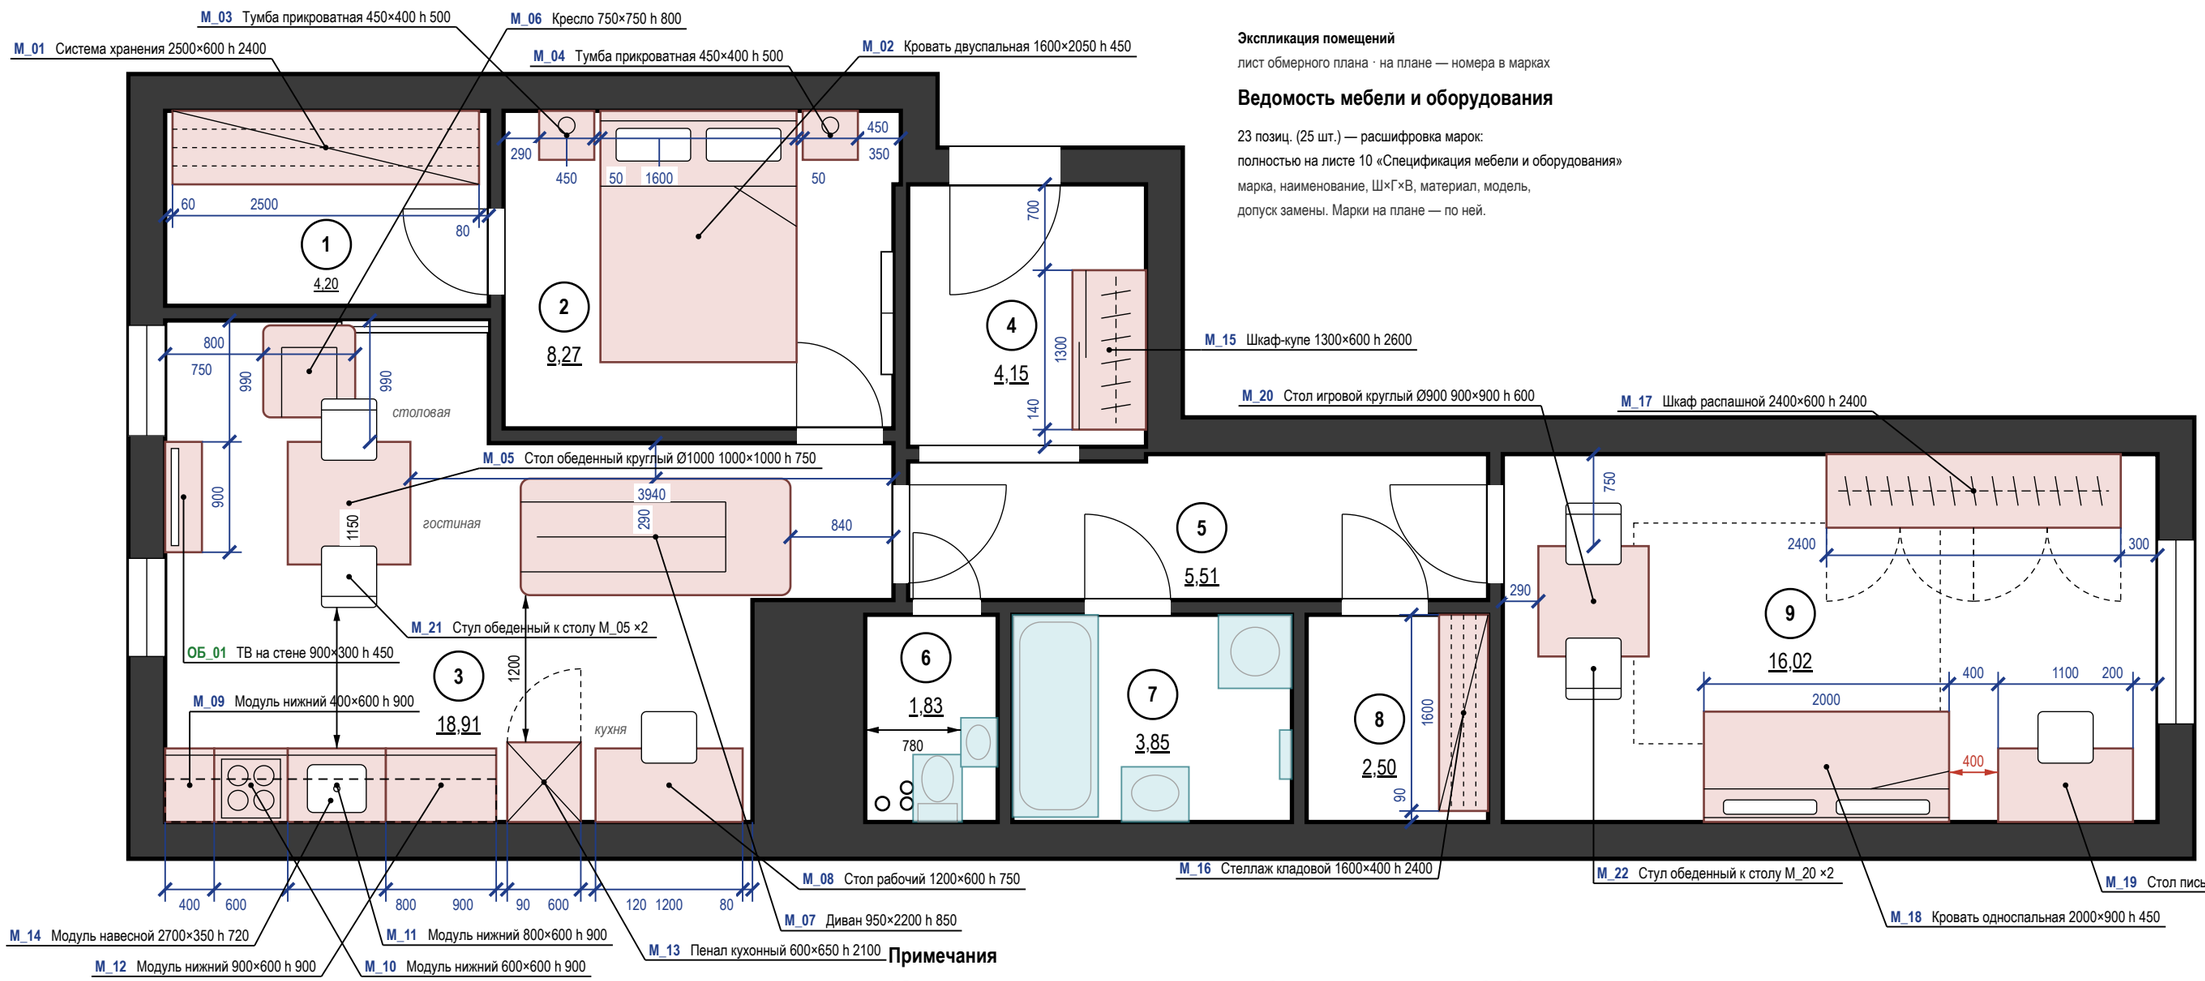

Экспликация помещений

лист обмерного плана · на плане — номера в марках

Ведомость мебели и оборудования

23 позиц. (25 шт.) — расшифровка марок:
полностью на листе 10 «Спецификация мебели и оборудования»
марка, наименование, Ш×Г×В, материал, модель,
допуск замены. Марки на плане — по ней.

Примечания

1. Размеры — в мм от чистовых поверхностей стен; размеры мебели уточнить после отделочных работ; общие указания — лист 2.
2. Отступ от стены, на плане не образмерен: М_06 — 40 мм.
3. Стулья обеденной группы (М_21 — 2 шт., М_22 — 2 шт.) показаны в рабочем положении, задвинутыми под столешницу на 150 мм.

					Проект: Квартира 65 м²			
	Лист	№ док.	Подпись	Дата	План размещения мебели и оборудования	Стадия	Лист	Листов
Дизайнер	Кырлан А.С.			21.10.26		П	9	80

Правка к этому листу

Поз.	Наименование и техническая характеристика	Тип, марка, обозначение документа, опросного листа	Код продукции	Поставщик	Ед. измерения	Кол.	Масса 1 ед., кг	Примечание
	Мебель встроенная и корпусная (изготовление по чертежам мебельщика)							
М_01	Система хранения: штанги, полки, ящики; каркас и полки — ЛДСП, декор «дуб натуральный»; Ш×Г×В 2500×600×2400 мм			изготовление на заказ	шт.	1		пом. 1; крепление к стене
М_09	Модуль нижний; корпус ЛДСП 16 мм, фасады МДФ эмаль; Ш×Г×В 400×600×900 мм			изготовление на заказ	шт.	1		пом. 3
М_10	Модуль нижний, варочная; корпус ЛДСП 16 мм, фасады МДФ эмаль; Ш×Г×В 600×600×900 мм			изготовление на заказ	шт.	1		пом. 3
М_11	Модуль нижний, мойка; корпус ЛДСП 16 мм, фасады МДФ эмаль; Ш×Г×В 800×600×900 мм			изготовление на заказ	шт.	1		пом. 3
М_12	Модуль нижний; корпус ЛДСП 16 мм, фасады МДФ эмаль; Ш×Г×В 900×600×900 мм			изготовление на заказ	шт.	1		пом. 3
М_13	Пенал кухонный, холодильник; корпус ЛДСП 16 мм, фасады МДФ эмаль; Ш×Г×В 600×650×2100 мм			изготовление на заказ	шт.	1		пом. 3
М_14	Модуль навесной; корпус ЛДСП 16 мм, фасады МДФ эмаль; Ш×Г×В 2700×350×720 мм			изготовление на заказ	шт.	1		пом. 3
М_15	Шкаф-купе; корпус ЛДСП, фасады — матовая эмаль в цвет стен (NCS S 1502-Y50R); Ш×Г×В 1300×600×2600 мм			изготовление на заказ	шт.	1		пом. 4
М_17	Шкаф распашной; корпус ЛДСП, фасады — матовая эмаль в цвет стен (Farrow & Ball No. 241); Ш×Г×В 2400×600×2400 мм			изготовление на заказ	шт.	1		пом. 9
	Мебель покупная							
М_02	Кровать двуспальная; мягкое изголовье, обивка — ткань, цвет NCS S 1500-N; Ш×Г×В 1600×2050×450 мм			аналог по характеристикам	шт.	1		пом. 2; замена ≤ габарита
М_03, М_04	Тумба прикроватная; шпон, дуб натуральный, матовое масло; Ш×Г×В 450×400×500 мм			аналог по характеристикам	шт.	2		пом. 2; замена ≤ габарита
М_05	Стол обеденный круглый Ø1000; шпон, дуб натуральный, матовое масло; Ш×Г×В 1000×1000×750 мм			аналог по характеристикам	шт.	1		пом. 3; замена ≤ габарита
М_06	Кресло; обивка — ткань, цвет NCS S 1500-N; Ш×Г×В 750×750×800 мм			аналог по характеристикам	шт.	1		пом. 3; замена ≤ габарита
М_07	Диван; обивка — ткань, цвет NCS S 1500-N; Ш×Г×В 950×2200×850 мм			аналог по характеристикам	шт.	1		пом. 3; замена ≤ габарита
М_08	Стол рабочий (кабинет); шпон, дуб натуральный, матовое масло; Ш×Г×В 1200×600×750 мм			аналог по характеристикам	шт.	1		пом. 3; замена ≤ габарита
М_21	Стул обеденный к столу М_05; обивка — ткань, цвет NCS S 1500-N; каркас — дуб натуральный; Ш×Г×В 450×500×820 мм			аналог по характеристикам	шт.	2		пом. 3; замена ≤ габарита
ОБ_01	ТВ на стене, тумба подвесная; шпон, дуб натуральный, матовое масло; Ш×Г×В 900×300×450 мм			аналог по характеристикам	шт.	1		пом. 3; замена ≤ габарита
М_16	Стеллаж кладовой; каркас и полки — ЛДСП, декор «дуб натуральный»; Ш×Г×В 1600×400×2400 мм			аналог по характеристикам	шт.	1		пом. 8; замена ≤ габарита
М_18	Кровать односпальная 900×2000; мягкое изголовье, обивка — ткань, цвет NCS S 1500-N; Ш×Г×В 2000×900×450 мм			аналог по характеристикам	шт.	1		пом. 9; замена ≤ габарита

Примечания

1. Позиции мебели совпадают с марками на плане расстановки; размеры Ш×Г×В — Ш вдоль стены, Г от стены.
2. Размеры и привязки плана расстановки — в мм от чистовых поверхностей стен: слой штукатурки 20 мм по блоку и 5 мм шпаклёвки по ГКЛ учтён; привязки — от стен и углов помещения, а не от другой мебели.
3. План расстановки не является документацией для изготовления мебели. Встроенная и корпусная мебель изготавливается по чертежам мебельщика после контрольного обмера (после штукатурки); «стена в стену» — с зазором 10 мм с каждой стороны или с компенсаторами; графы «Тип, марка» и «Код продукции» для неё не заполняются (ГОСТ 21.110-2013).
4. Покупные изделия — аналог по характеристикам: заменять только на изделия не больше указанного габарита и того же материала и цвета.
5. Материал и цвет, не указанные в данных изделия, приняты по концепции: тон дерева — по полу, обивка — по вторичному цвету палитры; образцы согласовать до заказа.
6. Масса 1 ед. для изделий до 25 кг не указывается. Техника — по монтажным схемам изготовителя; выводы — по листам ЭОМ и ВК.

					Проект: Квартира 65 м²
	Лист	№ док.	Подпись	Дата	Спецификация мебели и оборудования
Дизайнер	Кырлан А.С.			21.10.26	

Стадия	Лист	Листов
П	10	80

Правка к этому листу

Поз.	Наименование и техническая характеристика	Тип, марка, обозначение документа, опросного листа	Код продукции	Поставщик	Ед. измерения	Кол.	Масса 1 ед., кг	Примечание
M_19	Стол письменный; шпон, дуб натуральный, матовое масло; Ш×Г×В 1100×600×750 мм			аналог по характеристикам	шт.	1		пом. 9; замена ≤ габарита
M_20	Стол игровой круглый Ø900; шпон, дуб натуральный, матовое масло; Ш×Г×В 900×900×600 мм			аналог по характеристикам	шт.	1		пом. 9; замена ≤ габарита
M_22	Стул обеденный к столу M_20; обивка — ткань, цвет NCS S 1500-N; каркас — дуб натуральный; Ш×Г×В 450×500×820 мм			аналог по характеристикам	шт.	2		пом. 9; замена ≤ габарита
	Техника встраиваемая и бытовая, светильники под розетки							
	Варочная панель встраиваемая, электрическая, в модуле M_10			аналог по характеристикам	шт.	1		пом. 3; по схеме изготовителя
	Холодильник, в модуле M_13			аналог по характеристикам	шт.	1		пом. 3; по схеме изготовителя
	Стиральная машина, место по листу ВК (ОБ_02); Ш×Г 600×600 мм			аналог по характеристикам	шт.	1		пом. 7; по схеме изготовителя
	Торшер, у поз. M_06; абажур — ткань или опаловое стекло; лампа 3000 K			аналог по характеристикам	шт.	1		пом. 3; розетка — по плану розеток (ЭОМ)
	Текстиль							
T7	Портьеры-волна; лён 100 %; цвет Tikkurila H487; карниз 1820 мм, высота 2610 мм, сборка 2			аналог по характеристикам	шт.	2		пом. 9
T8	Тюль; полиэстер 100 %; цвет Tikkurila V503; карниз 1820 мм, высота 2610 мм, сборка 2,5			аналог по характеристикам	шт.	1		пом. 9
T9	Ковёр под кроватью; шерсть 100 %; цвет Tikkurila V484; 2500×1800 мм			аналог по характеристикам	шт.	1		пом. 9; с подложкой
T10	Подушки декоративные на кровать; букле (шерсть 60 %, полиэстер 40 %); цвет Farrow & Ball No. 229			аналог по характеристикам	шт.	3		пом. 9
T11	Подушки на кровать, акцент; хлопковый бархат 100 %; цвет Farrow & Ball No. 47			аналог по характеристикам	шт.	2		пом. 9
T12	Плед на кровать; шерсть мериноса 100 %; цвет Farrow & Ball No. 30			аналог по характеристикам	шт.	1		пом. 9
	Декор							
ДК3	Картина над кроватью: графика в паспарту, рама — дуб; 1000×700 мм; низ на 1300 мм от пола			аналог по характеристикам	шт.	1	4	пом. 9; крепление к стене
ДК4	Зеркало в рост в тонкой чёрной раме; рама — чёрный матовый; 600×1600 мм; низ на 300 мм от пола			аналог по характеристикам	шт.	1	12	пом. 9; крепление: анкер для пустотелых оснований, 4 шт.

					Проект: Квартира 65 м²			
	Лист	№ док.	Подпись	Дата	Спецификация мебели и оборудования (продолжение)	Стадия	Лист	Листов
Дизайнер	Кырлан А.С.			21.10.26		П	11	80

Правка к этому листу

Ведомость изделий

Марка	Наименование	Пом.	Ш×Г×В, мм	Корпус	Фасад	Кромка, мм скр./вид.	Кол.
M_01	Система хранения	1	2500×600×2400	ЛДСП 16	без фасадов; ящики — МДФ 18, эмаль матовая	0,4 / 2	1
M_15	Шкаф-купе	4	1300×600×2600	ЛДСП 16	рифлёные панели МДФ в алюминиевом профиле	0,4 / 1	1
M_16	Система хранения	8	1600×400×2400	ЛДСП 16	без фасадов; ящики — МДФ 18, эмаль матовая	0,4 / 2	1
M_17	Шкаф распашной	9	2400×600×2400	ЛДСП 16	МДФ 18, эмаль матовая	0,4 / 2	1
M_13	Пенал: холодильник	3	600×650×2100	ЛДСП 16	МДФ эмаль	0,4 / 1	1
M_12	Модуль нижний: ящики	3	900×600×900	ЛДСП 16	МДФ эмаль	0,4 / 1	1
M_14	Модуль навесной: полки, сушка	3	2700×350×720	ЛДСП 16	МДФ эмаль	0,4 / 1	1
M_11	Модуль нижний: мойка	3	800×600×900	ЛДСП 16	МДФ эмаль	0,4 / 1	1
M_10	Модуль нижний: ящики, варочная	3	600×600×900	ЛДСП 16	МДФ эмаль	0,4 / 1	1
M_09	Модуль нижний: ящики	3	400×600×900	ЛДСП 16	МДФ эмаль	0,4 / 1	1

Ведомость встраиваемой техники

Поз.	Прибор	Ниша, вырез, мм	Вентиляция	Питание	Схема
M_13	Холодильник отдельностоящий	проём 600, зазор сверху ≥ 50	по паспорту модели	розетка рядом, не за корпусом	по модели
M_11	Мойка врезная / подстольная с сифоном	вырез по шаблону, ориентир 700 × 480		смеситель — выводы ВК	по модели
M_10	Варочная панель индукционная, 60 см	вырез в столешнице 560 × 490		вывод кабеля под модулем	по модели
M_10	Вытяжка настенная, 60 см	низ ≥ 650 над панелью	воздуховод к вентканалу, короб до потолка	вывод кабеля в коробе	по модели

Ведомость фурнитуры

№	Фурнитура	Тип, размер	Изделия	Кол.
1	Полкодержатель с фиксацией	ø5 мм	M_01, M_15, M_16, M_17, M_14	140
2	Штанга овальная 30×15, L = 605	+ 2 держателя	M_01	2
3	Опора регулируемая с цоколем на клипсах	ход 20 мм	M_01, M_15, M_16, M_17	30
4	Анкер по основанию стены	по таблице крепежа	M_01, M_15, M_16, M_17, M_14	37
5	Уголок крепления к стене от опрокидывания	стальной	M_01, M_15, M_16, M_17, M_13	10
6	Система дверей купе: профиль, направляющие, ролики	на 2 двери	M_15	1
7	Ручка-профиль вертикальная	в цвет профиля	M_15	2
8	Штанга овальная 30×15, L = 626	+ 2 держателя	M_15	1
9	Полка для обуви выдвижная наклонная	ширина 626	M_15	3
10	Штанга выдвижная торцевая	L по глубине	M_16	1
11	Петля накладная 110° с доводчиком	чашка 35 мм	M_17, M_14, M_11	48
12	Штанга овальная 30×15, L = 936	+ 2 держателя	M_17	2
13	Штанга овальная 30×15, L = 456	+ 2 держателя	M_17	1
14	Опора кухонная регулируемая 100–120 мм	+ клипса цоколя	M_13, M_12, M_11, M_10, M_09	24
15	Направляющие полного выдвижения с доводчиком NL 500	пара	M_12, M_10, M_09	9
16	Ручка-профиль	латунь матовая	M_12, M_14, M_11, M_10, M_09	18
17	Сушка для посуды в шкаф	ширина 800	M_14	1
18	Навес регулируемый для навесного шкафа	пара на секцию	M_14	4
19	Шина монтажная	L = 2640	M_14	1

Примечания

1. Модели техники выбирает заказчик до изготовления мебели; ниши, вырезы и вентиляция — по монтажной схеме выбранной модели (условие гарантии), её номер вносится в ведомость.
2. Количество фурнитуры — по чертежам изделий; запас крепежа 5 %. Аналоги — по характеристикам (доводчик, нагрузка, ход).
3. Цвет корпусов, фасадов и профилей — по колерной карте проекта.


					Проект: Квартира 65 м²
	Лист	№ док.	Подпись	Дата	Ведомости изделий, техники и фурнитуры
Дизайнер	Кырлан А.С.			21.10.26	

Стадия	Лист	Листов
П	12	80


выпуск 09.10.2026 № da691793fd · стр. 12 из 80

Правка к этому листу


Фрагмент 1. Кухня-гостиная (пом. 3)

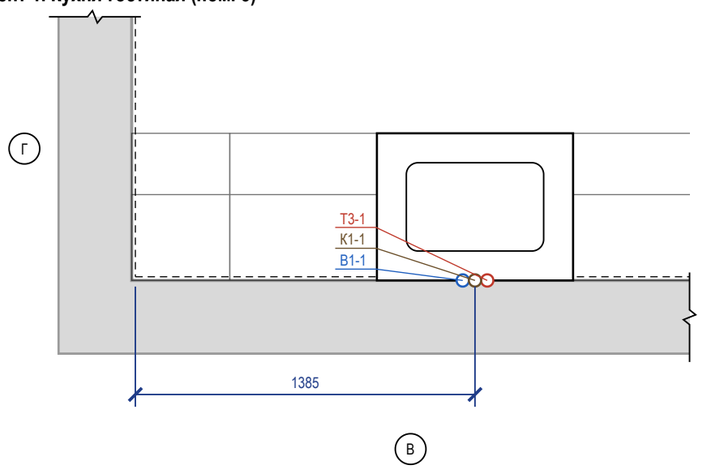

Фрагмент 2. Санузел (пом. 6)

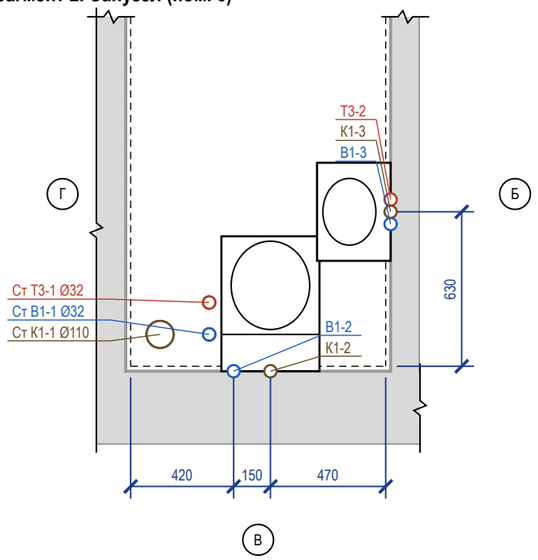

Фрагмент 3. Ванная (пом. 7)

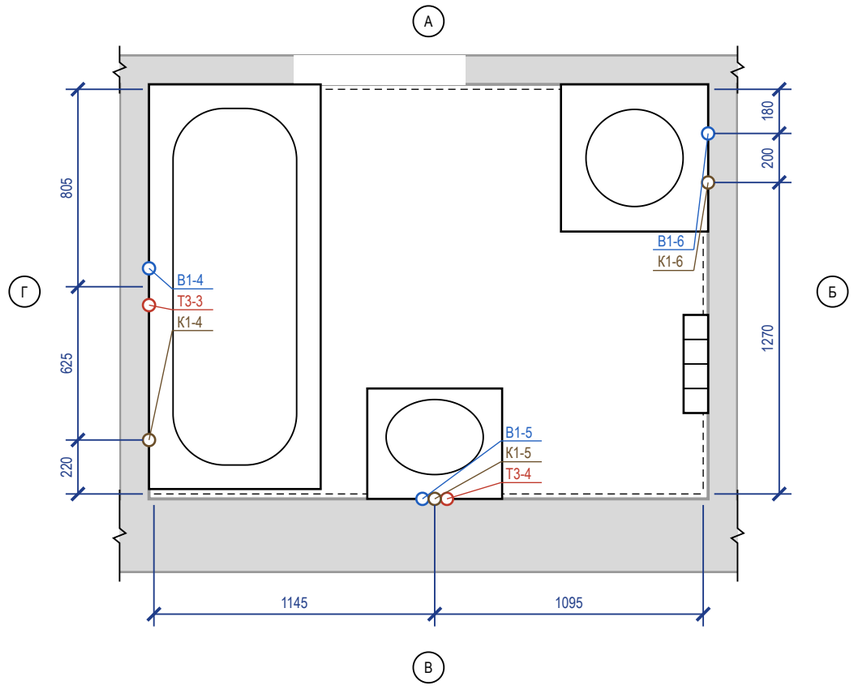

Ведомость привязок выводов

Код	Прибор	Ø	H, мм	Привязка от чист. стен, мм	Прим.
В1-1	С_01 мойка кухонная	½"	550	ст. В: 1335 от Г	межос. 100
Т3-1	С_01 мойка кухонная	½"	550	ст. В: 1435 от Г	межос. 100
К1-1	С_01 мойка кухонная	Ø50	400	ст. В: 1385 от Г	
В1-2	С_02 унитаз подвесной	½"	1000	ст. В: 420 от Г	в раме инсталляции
К1-2	С_02 унитаз подвесной	Ø110	220	ст. В: 470 от Б	
В1-3	С_03 умывальник	½"	550	ст. Б: 580 от В	межос. 100
Т3-2	С_03 умывальник	½"	550	ст. Б: 680 от В	межос. 100
К1-3	С_03 умывальник	Ø50	500	ст. Б: 630 от В	
В1-4	С_04 ванна	½"	800	ст. Г: 730 от А	межос. 150
Т3-3	С_04 ванна	½"	800	ст. Г: 770 от В	межос. 150
К1-4	С_04 ванна	Ø50	50	ст. Г: 220 от В	
В1-5	С_05 умывальник	½"	550	ст. В: 1095 от Г	межос. 100
Т3-4	С_05 умывальник	½"	550	ст. В: 1045 от Б	межос. 100
К1-5	С_05 умывальник	Ø50	500	ст. В: 1095 от Б	
В1-6	ОБ_02 стиральная машина	½"	800	ст. Б: 180 от А	кран машины
К1-6	ОБ_02 стиральная машина	Ø50	600	ст. Б: 380 от А	

Условные обозначения

- вывод В1 (код — в ведомости привязок)
- вывод Т3 (код — в ведомости привязок)
- вывод К1 (код — в ведомости привязок)
- сантехприбор по расстановке (габарит модели)
- чистовая поверхность стены (от неё привязки)
- стояк «Ст К1-N / Ст В1-N» (ГОСТ 21.601), Ø мм
- линия обрыва (граница фрагмента)
- А — обозначение стены А–Г (как на развёртках)

Примечания

1. Привязки выводов даны от чистовых поверхностей стен (облицовка на сторону: кухня-гостиная — 15 мм (по данным); санузел — 20 мм (по данным); ванная — 20 мм (по данным)); эти же грани — на развёртках и в раскладке плитки. Высоты — от чистого пола помещения.
2. До черновой разводки сверить по паспорту выбранного прибора (смеситель, инсталляция, сифон).
3. Горячая вода (Т3) — слева от холодной (В1), если смотреть на прибор. Допуск установки выводов: ±5 мм в группе, ±20 мм у отдельно стоящих.
4. Расчёт систем водоснабжения и канализации и подбор оборудования выполняет проектная организация; лист задаёт места и высоты выводов.
5. Стояки в коробах/шахтах не замоноличивать; стояк К1 в коробе — звукоизоляция стояка в коробе без жёсткого контакта с трубой; к арматуре и ревизиям — люк не меньше 300×400.


					Проект: Квартира 65 м²
	Лист	№ док.	Подпись	Дата	План выводов сантехники
Дизайнер	Кырлан А.С.			21.10.26	

Стадия	Лист	Листов
П	13	80


выпуск 09.10.2026 № da691793fd · стр. 13 из 80

Правка к этому листу


План квартиры (М 1:400)

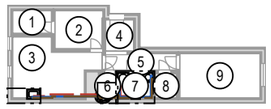


Фр. 1. Кухня-гостиная (М 1:20)

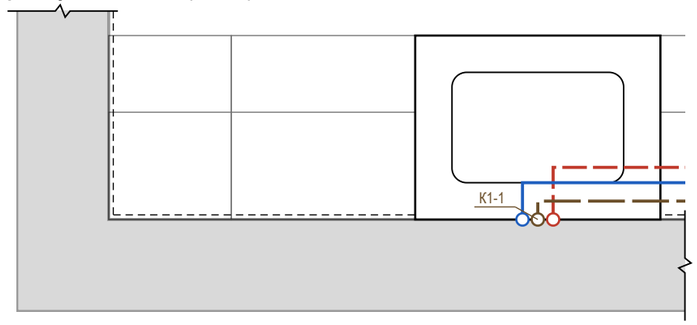

Фр. 3. Ванная (М 1:20)

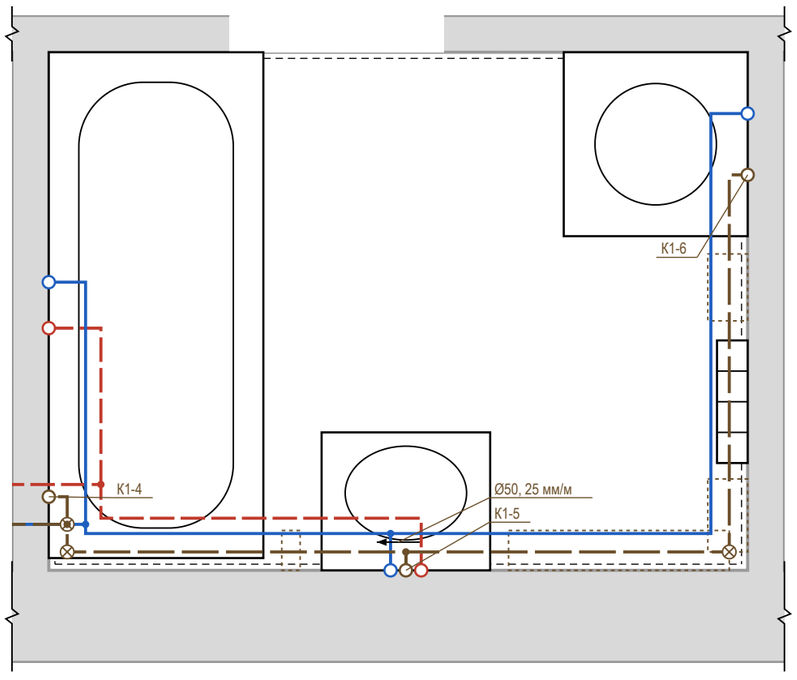

Фр. 2. Санузел (М 1:20)

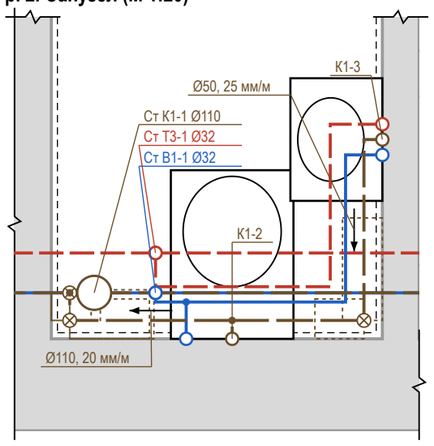

Условные обозначения

- В1 — водопровод хозяйственно-питьевой (ХВС), PP-R Ø20
- Т3 — горячее водоснабжение, подача (ГВС), PP-R Ø20
- К1 — канализация бытовая
- направление уклона К1 / пола: Ø, мм на 1 м
- ⊗ ревизия (прочистка) К1 — доступ сохранить
- • тройник (ответвление к прибору)
- короб К1 над чистым полом (ГКЛВ под плитку)
- ○ вывод В1 (код — в ведомости привязок)
- ○ вывод Т3 (код — в ведомости привязок)
- ○ вывод К1 (код — в ведомости привязок)
- сантехприбор по расстановке (габарит модели)
- ○ стояк «Ст К1-N / Ст В1-N» (ГОСТ 21.601), Ø мм
- линия обрыва (граница фрагмента)
- граница фрагмента на плане (Фр. N)

Профиль выпусков К1 (до врезки в стояк)

Выпуск	Прибор	Ø	L, м	i, мм/м	Δh, мм	Прокладка, мм
К1-2	С_02 унитаз подвесной	Ø110	0,76	20	15	короб 160×140
К1-6	ОБ_02 стиральная машина	Ø50	4,66	25	117	короб 200×110
К1-1	С_01 мойка кухонная	Ø50	4,60	25	115	над полом за приборами
К1-5	С_05 умывальник	Ø50	2,38	25	59	над полом за приборами
К1-3	С_03 умывальник	Ø50	1,78	25	45	короб 130×110
К1-4	С_04 ванна	Ø50	1,27	25	32	в полу: нужно 157 > 90 — решение!

Короб h×b: h — от чистого пола, b — от чистовой стены. Стяжка 90 мм — лист полов.

Узел ввода В1, Т3 (схема, без масштаба)



⊗ Ст К1-1: ревизия на стояке — люк в коробе

Примечания

1. Трассы принципиальные, построены от стояков вдоль стен помещений; фактическое положение фиксируется исполнительной схемой с привязками (фото с рулеткой) до закрытия.
2. Уклон К1 не менее 1/d и не более 150 мм/м (СП 30.13330.2020, п. 19.1), приняты практические уклоны; поворот — двумя отводами 45°, ревизия после поворота, доступ сохранить. Стояк К1 в коробе — звукоизоляция стояка в коробе, без жёсткого контакта короба с трубой.
3. Решение по К1: стяжка 90 мм не укрывает трубы (нужно Ø + Δh + 45 мм) — выпуски идут над чистым полом вдоль стен: К1-1, К1-5 — за приборами и в раме инсталляции; К1-2, К1-6, К1-3 — в коробе ГКЛВ под плитку (размеры в профиле). Короба — на развёртках; отметку низа врезки в стояк замерить до черновых работ.
4. На каждом вводе В1 и Т3 — кран шаровой, фильтр, счётчик, обратный клапан; доступ через люк не меньше 300×400. Водопровод — в штробе стен или в коробах; трубы испытать давлением до закрытия (акт скрытых работ).
5. Расчёт систем, диаметры магистралей и подбор оборудования выполняет проектная организация; врезка и перенос стояков — по согласованию с управляющей организацией. Арматуру и привязки сверить по паспортам приборов.

					Проект: Квартира 65 м²
	Лист	№ док.	Подпись	Дата	
Дизайнер	Кырлан А.С.			21.10.26	Схема разводки водопровода и канализации
					Стадия: П; Лист: 14; Листов: 80

Правка к этому листу

Поз.	Наименование и техническая характеристика	Тип, марка, обозначение документа	Код продукции	Поставщик	Ед. изм.	Кол.	Масса 1 ед., кг	Примечание
	Санитарные приборы							
1	Ванна акриловая 1650×700 мм, с каркасом, экраном и отверстием слив-перелив	Ravak Classic C541000000		выбор заказчика	шт	1		С_04
2	Унитаз подвесной безободковый, с сиденьем микролифт, крепёж и звукоизолирующая прокладка	Jacob Delafon Struktura EDF102-00		выбор заказчика	шт	1		С_02
3	Инсталляция для подвесного унитаза: рама высотой 1120 мм, бачок, клавиша смыва (ось клавиши 1050 мм от чистого пола)	аналог		выбор заказчика	шт	1		С_02; короб ГКЛВ
4	Умывальник подвесной 400×300 мм, с отверстием под смеситель и переливом	Roca The Gap 7.3274.7.400.0		выбор заказчика	шт	1		С_03
5	Умывальник подвесной 550×450 мм, с отверстием под смеситель и переливом	Roca The Gap 7.3274.7.400.0		выбор заказчика	шт	1		С_05
6	Мойка кухонная 800×600 мм, с переливом	мойка врезная 780×510 в шкафу М_11		с кухонной мебелью	шт	1		С_01
7	Полотенцесушитель электрический, IP44, с терморегулятором	аналог		выбор заказчика	шт	1		С_06
	Смесители, сифоны и арматура приборов							
8	Смеситель для ванны настенный однорычажный, межосевое 150 мм, с душевым набором (лейка, шланг, держатель)	аналог		выбор заказчика	шт	1		С_04
9	Смеситель для умывальника однорычажный, с донным клапаном	аналог		выбор заказчика	шт	2		С_03, С_05
10	Смеситель кухонный однорычажный, высокий излив	аналог		выбор заказчика	шт	1		С_01
11	Обвязка ванны слив-перелив Ø40/50 с сифоном	аналог		выбор заказчика	шт	1		С_04
12	Сифон для умывальника бутылочный Ø32/40–50, с гофрой к выпуску	аналог		выбор заказчика	шт	2		С_03, С_05
13	Сифон для мойки Ø40/50	аналог		выбор заказчика	шт	1		С_01
14	Сифон для стиральной машины встраиваемый в стену Ø50, с обратным клапаном	аналог		выбор заказчика	шт	1		ОБ_02
15	Кран угловой ½"×½" с гибкой подводкой 40 см (умывальники, мойка)	аналог		выбор заказчика	шт	6		по 2 на прибор
16	Кран шаровой угловой ½"×¾" для подключения стиральной и посудомоечной машины	аналог		выбор заказчика	шт	1		ОБ_02
	Трубопроводы							
17	Труба полипропиленовая PP-R PN20 Ø20×3,4 (В1)	ГОСТ 32415-2013		выбор заказчика	м	18	0,17	11,8 + 4,3 + 10 %
18	Труба PP-R, армированная стекловолокном, PN20 Ø20×2,8 (Т3)	ГОСТ 32415-2013		выбор заказчика	м	13	0,15	9,3 + 2,5 + 10 %
19	Труба канализационная ПП Ø50 (К1)	ГОСТ 32414-2013		выбор заказчика	м	14		10,5 + 2,0 + 10 %
20	Труба канализационная ПП Ø110 (К1)	ГОСТ 32414-2013		выбор заказчика	м	1,5		0,8 + 0,2 + 10 %
	Фасонные части и выводы							
21	Отвод канализационный ПП 45° Ø50	ГОСТ 32414-2013		выбор заказчика	шт	20		2 шт. на поворот
22	Отвод канализационный ПП 45° Ø110	ГОСТ 32414-2013		выбор заказчика	шт	6		2 шт. на поворот
23	Тройник канализационный ПП 45° (врезки ветвей)	ГОСТ 32414-2013		выбор заказчика	шт	5		
24	Ревизия канализационная ПП (после поворота трассы)	ГОСТ 32414-2013		выбор заказчика	шт	8		доступ сохранить
25	Фитинги PP-R Ø20: тройники, угольники 90° (ветви и повороты В1, Т3)	ГОСТ 32415-2013		выбор заказчика	шт	29		
26	Водорозетка PP-R Ø20×½" настенная, с креплением	ГОСТ 32415-2013		выбор заказчика	шт	10		коды — лист выводов
	Узлы ввода, люки, короба							
27	Кран шаровой латунный Ду15 PN16 (отключение ввода)	аналог		выбор заказчика	шт	2		Ст В1-1, Ст Т3-1
28	Фильтр сетчатый косой Ду15	аналог		выбор заказчика	шт	2		
29	Счётчик воды крыльчатый Ду15 (ХВ, ГВ), с поверкой	аналог		выбор заказчика	шт	2		пломба УК
30	Клапан обратный Ду15	аналог		выбор заказчика	шт	2		
31	Люк ревизионный нажимной под плитку 300×400 мм	аналог		выбор заказчика	шт	1		к стоякам и арматуре
32	Звукоизоляция стояка К1 в коробе: рулонный звукоизоляционный материал ≥ 10 мм, обмотка стояка на высоту этажа	аналог		выбор заказчика	м	2,7		Ст К1-1
33	Короб К1 над полом: профиль ПН/ПС, ГКЛВ 12,5 мм под плитку	аналог		выбор заказчика	м	2,9		сечение — лист разводки


Примечания

1. Форма 1 ГОСТ 21.110-2013, ширины граф изменены по п. 4.1. «Аналог» — аналог по характеристикам: модели внести до черновых работ, привязки выводов сверить по паспортам.
2. Бытовая техника не входит (показана арматура подключения), мойка — в комплекте кухни. Длины труб — трасса листа разводки + подъёмы + 10 %.
3. Стояк К1 в коробе — звукоизоляция стояка в коробе без жёсткого контакта короба с трубой.
4. Расчёт систем водоснабжения и канализации, диаметры магистралей и подбор оборудования выполняет проектная организация.

					Проект: Квартира 65 м²
	Лист	№ док.	Подпись	Дата	Спецификация сантехнического оборудования
Дизайнер	Кырлан А.С.			21.10.26	

Стадия	Лист	Листов
П	15	80

Правка к этому листу

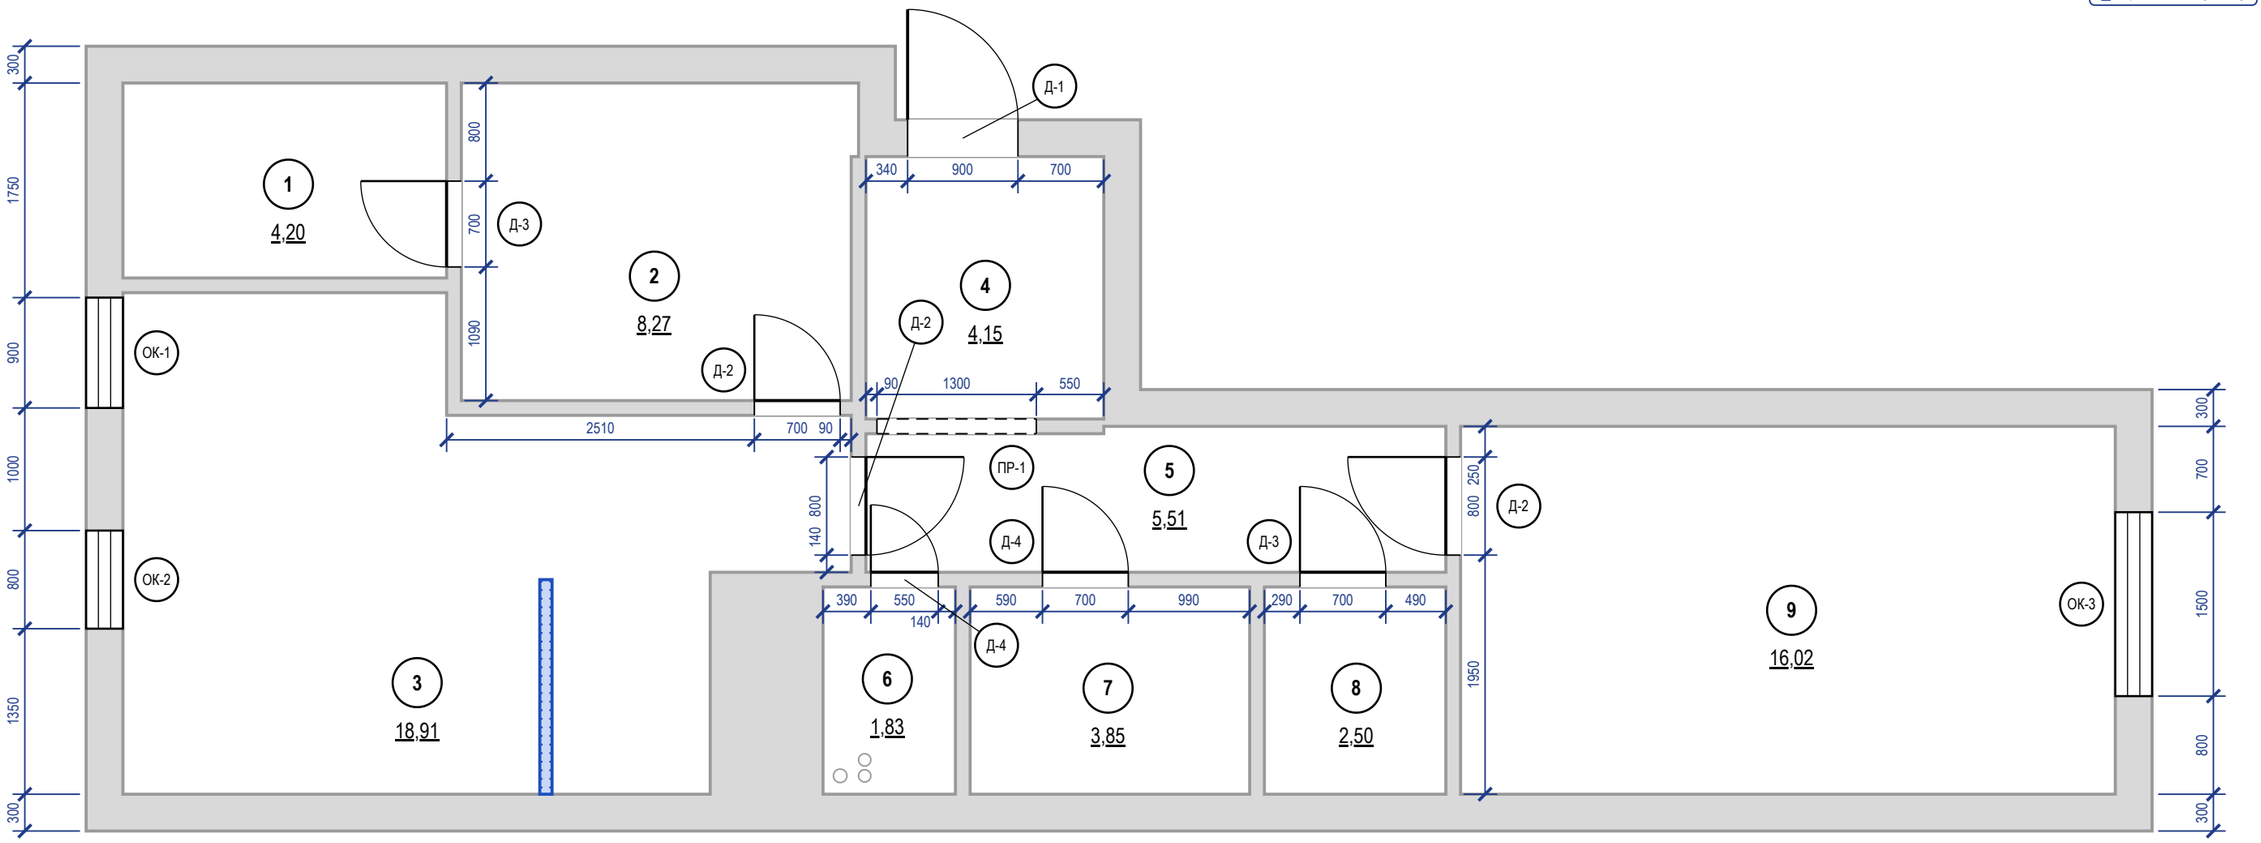

Ведомость заполнения проёмов

Марка	Наименование, обозначение	Проём ш×в, мм	Кол.	Откр.	Отделка полотна	Фурнитура	Прим.
Д-1	Блок дверной входной, ГОСТ 31173-2016	900×2100	1	П	в комплекте блока	в комплекте блока (замки, глазок)	наружу
Д-2	Дверь скрытого монтажа, ТУ изготовителя	700×2100	3	П, П, Л	S 1502-Y50R — пом. 2, S 1002-Y50R — пом. 3; S 1502-Y50R — пом. 5, S 1002-Y50R — пом. 3; S 1502-Y50R — пом. 5, No. 241 — пом. 9	скрытые петли 3D, магнитный замок	
Д-3	Дверь скрытого монтажа, ТУ изготовителя	700×2100	2	Л, П	V503 — пом. 1, S 1502-Y50R — пом. 2; S 1502-Y50R пом. 5, S 0502-Y — пом. 8	скрытые петли 3D, магнитный замок	
Д-4	Дверь скрытого монтажа, ТУ изготовителя	550×2100	2	П, П	S 1502-Y50R — пом. 5, в тон облицовки — пом. 6; S 1502-Y50R — пом. 5, в тон облицовки — пом. 7	скрытые петли 3D, магнитный замок, фиксатор WC	порог 15
ПР-1	Портал без заполнения	1300×2100	1				б/п
ОК-1	Блок оконный, ГОСТ 23166-2021	900×1600	1				низ 800
ОК-2	Блок оконный, ГОСТ 23166-2021	800×1600	1				низ 800
ОК-3	Блок оконный, ГОСТ 23166-2021	1500×1600	1				низ 800

Примечания

1. Размеры проёмов и привязки — в миллиметрах от чистых граней стен до отделки; привязка — от угла того помещения, со стороны которого стоит размер. Размер в ведомости — ширина × высота проёма от чистого пола 0,000. Откос от угла помещения до проёма с коробкой — не менее 50 мм.
2. Марки в кружках — типы заполнения проёмов (ГОСТ 21.501-2018, п. 5.3.2); одна марка — один типоразмер; количество сверено с планом.
3. Открывание: Л — петли слева, П — справа, если смотреть со стороны, куда открывается полотно (на себя).
4. Скрытые двери (Д-2…Д-4): проём замерить в чистоте; блок заказать до штукатурки (≈ 30 дн.), короб ставить до штукатурки; полотно навесить после чистовой отделки, красить в цвет стен. Порядок практика монтажа, изготовитель подтверждает.
5. Д-2…Д-4 — существующие проёмы, до техзаключения не расширять.
6. Размеры проёмов и привязки сняты со скана плана заказчика и на объекте не замерены (обмерный план — лист 3).
7. Экспликация помещений — лист 3; в марках помещений — номер и площадь, м².
8. Марки Д-2, Д-4: разные типоразмеры под одной маркой — развести марки.

					Проект: Квартира 65 м²			
	Лист	№ док.	Подпись	Дата	План размещения дверей	Стадия	Лист	Листов
Дизайнер	Кырлан А.С.			21.10.26		П	16	80

выпуск 09.10.2026 № da691793fd · стр. 16 из 80

Правка к этому листу



Ведомость потолков

Пом.	Марка	Конструкция	Низ / верх ниши	S, м²	Q
1		по плите, окраска	+2,700	4,20	
2		по плите, окраска	+2,700	8,27	
3		по плите, окраска	+2,700	18,91	
4		по плите, окраска	+2,700	4,15	
5		по плите, окраска	+2,700	5,51	
6		по плите, окраска	+2,700	1,83	
7		по плите, окраска	+2,700	3,85	
8		по плите, окраска	+2,700	2,50	
9		по плите, окраска	+2,700	16,02	
		Итого		**65,24**	

Ведомость вырезов и закладных в потолке

Марка	Устройство	Кол.	Пом.
	Светильник встраиваемый (марки — план освещения)	11	4, 5, 6, 7, 9
	Светильник накладной (марки — план освещения)	6	1, 2, 3, 8
	Светильник подвесной (марки — план освещения)	1	3
ИП2	Извещатель дымовой	3	2, 3, 9

Примечания

1. За отметку ±0,000 принят уровень чистого пола сухих помещений (готовое покрытие), а не существующего пола; пол пом. 6, 7 — −0,015; верх плиты перекрытия −0,064 — расчётный по пирогу пола, не замерен; существующий пол снимается до плиты, его отметка не замерена. Отметки в прямоугольниках — низ потолка; низ плиты перекрытия +2,700. Марка потолка — одна конструкция и отметка на весь альбом.
2. Светильники и потолочные устройства — подложка с планов освещения, слаботочных систем и вентиляции (положение — по ним); вырезы и закладные — по ведомости на листе, до обшивки; отверстия не совмещать с профилями.
3. Пом. 1, 2, 3, 4, 5, 6, 7, 8, 9 — потолок по плите без подвесной системы; отделка — по ведомости отделки.

	Лист	№ док.	Подпись	Дата
Дизайнер	Кырлан А.С.			21.10.26


Проект: Квартира 65 м²

План потолков

Стадия	Лист	Листов
П	17	80

выпуск 09.10.2026 № da691793fd · стр. 17 из 80

Правка к этому листу

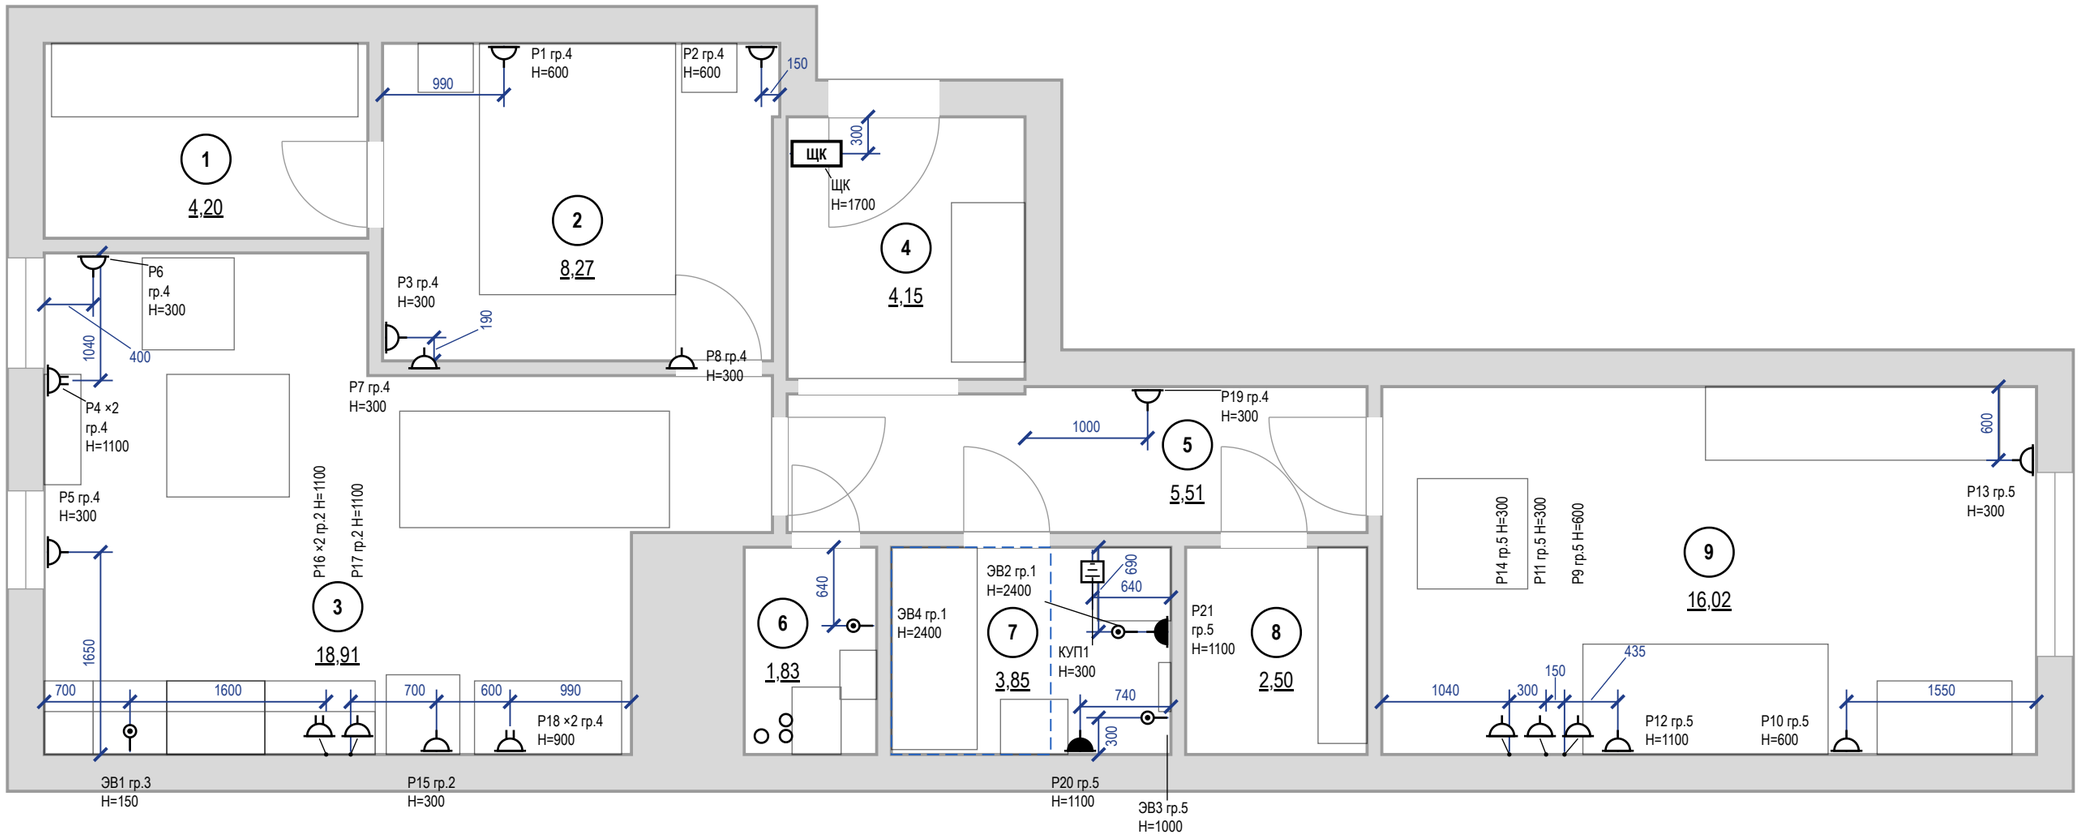


Примечания

1. За отметку 0,000 принят уровень чистого пола. Высоты Н — от чистого пола до оси изделия; привязки — от чистовой грани стены до оси механизма (у рамки на несколько постов — до оси рамки).
2. Высота установки, не указанная на плане: розетки — 300 мм от чистого пола; выводы кабеля — по паспорту прибора.
3. Розетки в санузле — только вне зон 0–2 (ПУЭ 7.1.48, ГОСТ Р 50571.7.701-2024), IP44, через УЗО 30 мА.
4. Розеточные и мокрые линии — через УЗО или дифавтомат с током утечки не более 30 мА (ПУЭ 7.1.79); в санузле выполнить ДСУП (ПУЭ 7.1.87–7.1.88).
5. Кабель — медный, исполнение нг(А)-LS (ГОСТ 31565-2012); скрытая прокладка только горизонтально и вертикально, фактические трассы зафиксировать исполнительной схемой до закрытия отделкой.
6. Расчёт нагрузок, токов КЗ, селективности и сечений — по проекту ЭОМ организации с допуском СРО; лист задаёт состав, расположение и группы.
7. Выводы кухонной техники — после утверждения проекта кухни (ориентировочно); привязки выводов даны от осей модулей гарнитура и пересматриваются вместе с проектом кухни.
8. Ведомости электроточек, изделий, светильников и расшифровка клавиш — лист «Ведомость электроточек и изделий».

					Проект: Квартира 65 м²
	Лист	№ док.	Подпись	Дата	
Дизайнер	Кырлан А.С.			21.10.26	План розеток и электровыводов

Стадия	Лист	Листов
П	18	80

Правка к этому листу

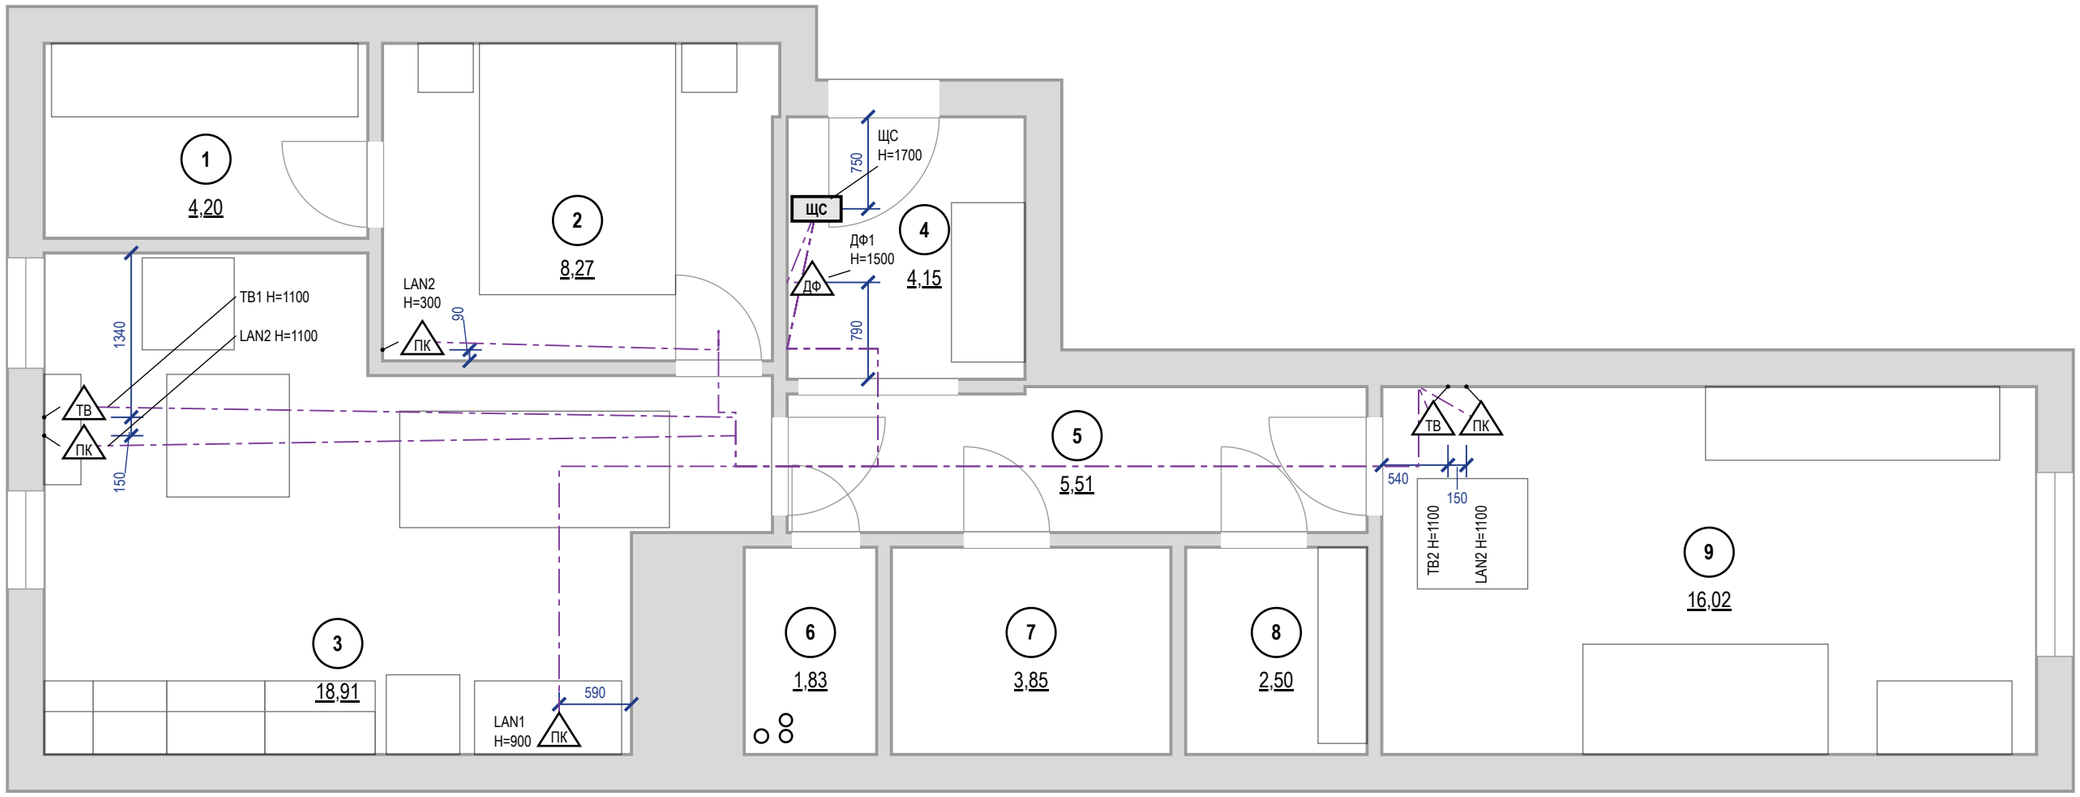


Примечания

1. За отметку 0,000 принят уровень чистого пола. Высоты H — от чистого пола до оси изделия; привязки — от чистовой грани стены до оси механизма (у рамки на несколько постов — до оси рамки).
2. Высота установки, не указанная на плане: розетки LAN и ТВ — 300 мм от чистого пола.
3. Слаботочные кабели — отдельно от силовых: в своей трубе или лотке, при параллельной прокладке не ближе 100 мм к силовым, пересечения под прямым углом; каждую точку — отдельным кабелем от ЩС без скруток.
4. Трассы на листе — принципиальные; фактические зафиксировать исполнительной схемой до закрытия отделкой. Силовые линии, УЗО 30 мА, ДСУП, кабель нг(A)-LS — по листам розеток и щита.
5. Проект силовой части и расчёт токов КЗ — по проекту ЭОМ; слаботочная часть согласуется с провайдером и управляющей компанией (домофон, коллективное ТВ).

					Проект: Квартира 65 м²
	Лист	№ док.	Подпись	Дата	
Дизайнер	Кырлан А.С.			21.10.26	План слаботочных сетей
					Стадия: П; Лист: 19; Листов: 80

выпуск 09.10.2026 № da691793fd · стр. 19 из 80

Правка к этому листу

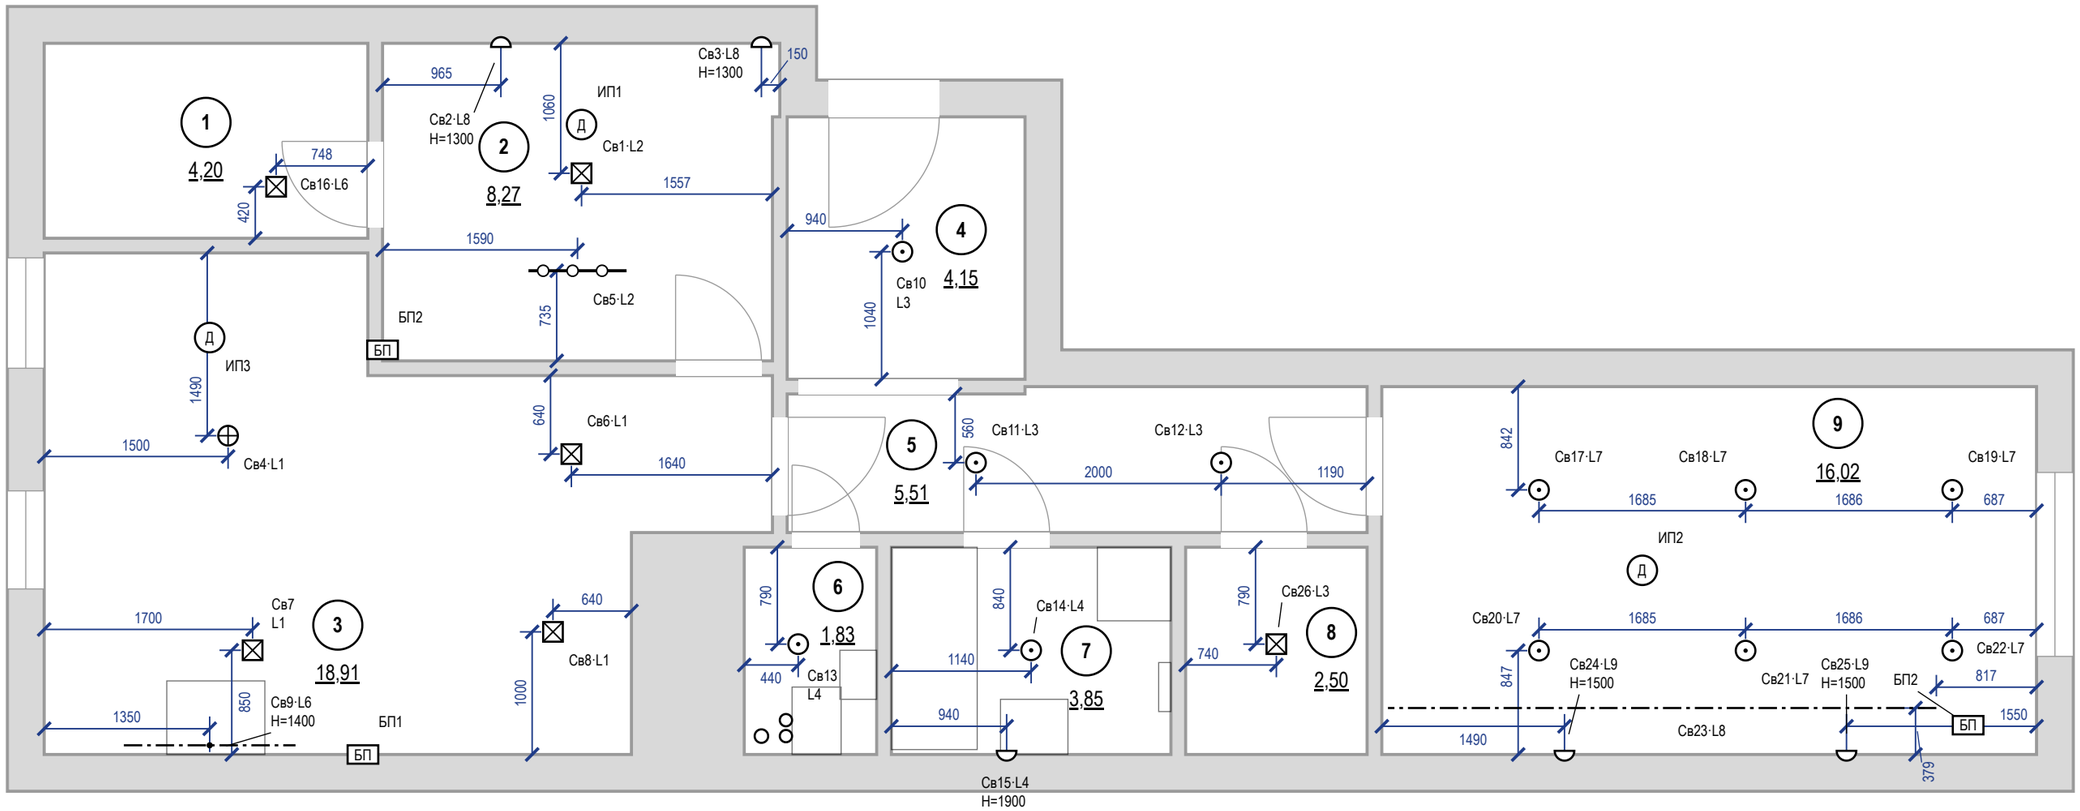

Примечания

1. За отметку 0,000 принят уровень чистого пола. Высоты H — от чистого пола до оси изделия; привязки — от чистовой грани стены до оси механизма (у рамки на несколько постов — до оси рамки).
2. Высота установки, не указанная на плане: светильники — на потолке; настенные — по отметке H у знака. Привязки — до оси светильника от чистовой грани стены, по рядам.
3. Освещённость: Ен — СанПиН 1.2.3685-21, табл. 5.52 (на полу); Ф треб. = Ен·S/(U·MF) при U = 0,5 и MF = 0,71 (СП 52.13330.2016, табл. 4.3) — оценка, не светотехнический расчёт. Декоративная подсветка в Ф не входит.
4. Во влажных помещениях — светильники не ниже IP44; в зонах 0–2 ванной — по ГОСТ Р 50571.7.701-2024 (зона 1 — IPX5).
5. Розеточные и мокрые линии — через УЗО или дифавтомат с током утечки не более 30 мА (ПУЭ 7.1.79); в санузле выполнить ДСУП (ПУЭ 7.1.87–7.1.88).
6. Кабель — медный, исполнение нг(A)-LS (ГОСТ 31565-2012); скрытая прокладка только горизонтально и вертикально, фактические трассы зафиксировать исполнительной схемой до закрытия отделкой.
7. Расчёт нагрузок, токов КЗ, селективности и сечений — по проекту ЭОМ организации с допуском СРО; лист задаёт состав, расположение и группы.
8. Ведомость светильников — лист «Ведомость электроточек и изделий».

					Проект: Квартира 65 м²
	Лист	№ док.	Подпись	Дата	План освещения
Дизайнер	Кырлан А.С.			21.10.26	Стадия: П; Лист: 20; Листов: 80

Правка к этому листу

Спецификация светильников

Поз.	Марки	Наименование	Установка	Кол.	P, Вт	Σ P, Вт	Ф, лм	Тц, К	Ra	Угол, °	IP	Дим.	Группа	Пом.
1	Св16	Потолочный накладной	на потолке, засветка стены	1	10	10	900	3000	90	—	20	—	L6	1
2	Св1	Потолочный накладной	на потолке	1	36	36	3200	2700	90	—	20	—	L2	2
3	Св5	Трековая система	на потолке	2	12	24	900	2700	90	—	20	—	L2	2
4	Св2, Св3	Настенный (бра)	на стене, H=1300	2	4	8	250	2700	90	—	20	—	L8	2
5	Св4	Подвесной	подвес	1	24	24	2400	3000	90	—	20	—	L1	3
6	Св6	Потолочный накладной	на потолке	1	18	18	1800	3000	90	—	20	—	L1	3
7	Св7	Потолочный накладной	на потолке	1	12	12	1100	3000	90	—	20	—	L1	3
8	Св8	Потолочный накладной	на потолке	1	12	12	1000	4000	90	—	20	—	L1	3
9	Св9	Линейный настенный	под верхними шкафами, H=1400	1	18	18	1300	3000	90	—	20	—	L6	3
10	Св10–Св12	Встраиваемый точечный	встраиваемый	3	9	27	800	3000	90	—	20	—	L3	4, 5
11	Св13	Встраиваемый точечный	встраиваемый	1	6	6	500	3000	90	—	20	—	L4	6
12	Св14	Встраиваемый точечный	встраиваемый	1	9	9	700	3000	90	—	44	—	L4	7
13	Св15	Настенный (бра)	над зеркалом, H=1900	1	6	6	400	3000	90	—	44	—	L4	7
14	Св26	Потолочный накладной	на потолке	1	9	9	600	3000	90	—	20	—	L3	8
15	Св17–Св22	Встраиваемый точечный	встраиваемый	6	12	72	1050	2700	90	—	20	—	L7	9
16	Св23	Лента светодиодная 24 В	в коробе, профиль с рассеивателем	12,3 м	9,6/м	118,1	900/м	2700	90	—	20	да	L8	9
17	Св24, Св25	Настенный (бра)	на стене, H=1500	2	6	12	400	2700	90	60	20	—	L9	9
		Итого		**26 шт + 12,3 м**		**421,1**								

LED-ленты, линейные светильники и блоки питания

Марка	Пом.	L, м	U, В	Вт/м	Σ P, Вт	БП	P БП, Вт	Загр., %	Питание	Доступ к БП
Св5	2	0,8	24	—	24	БП2	200	59	встроенный ввод	люк 300×300 в коробе У1 у окна
—	3	2,5	24	—	18	БП1	60	30	встроенный ввод	H=2300
Св23	9	12,3	24	9,6	118,1	БП2	200	59	с двух концов	люк 300×300 в коробе У1 у окна

Сценарии освещения

Пом.	Сценарий	Группы и уровни, %	Чем включается
9	Вечер	L7 споты — 0; L8 подсветка короба — 100; L9 бра — 100	S4, S5, S6

Слои света

общий — равномерный свет помещения, по норме освещённости

рабочий — местный свет задачи: столешница, зеркало, чтение у кровати

акцентный — подсветка потолка, стен и ниш; не входит в поток общего света

Слои света по помещениям

Пом.	Помещение	Слои света и группы включения (марки светильников)	Тц, К	Ra	Σ P, Вт	Сцен.
1	Гардеробная	общий — L6 (Св16)	3000	90	10	—
2	Спальня	общий — L2 (Св1, Св5); рабочий — L8 (Св2, Св3)	2700	90	68	—
3	Кухня-гостиная	общий — L1 (Св4, Св6–Св8); рабочий — L6 (Св9)	3000 / 4000	90	84	—
4	Прихожая	общий — L3 (Св10)	3000	90	9	—
5	Коридор	общий — L3 (Св11, Св12)	3000	90	18	—
6	Санузел	общий — L4 (Св13)	3000	90	6	—
7	Ванная	общий — L4 (Св14); рабочий — L4 (Св15)	3000	90	15	—
8	Кладовая	общий — L3 (Св26)	3000	90	9	—
9	Детская	общий — L7 (Св17–Св22); рабочий — L9 (Св24, Св25); акцентный — L8 (Св23)	2700	90	202,1	1


Примечания

1. Позиции и марки Св — те же, что на плане освещения (лист 20) и в ведомости светильников (лист «Ведомость электроточек и изделий»); группы L — по плану выключателей (лист 22).
2. Модели светильников не назначены: подбор по графам спецификации — поток, Тц, Ra, угол, IP и диммирование не хуже указанных, мощность не больше. IP 20 — сухие помещения.
3. Длина LED-ленты в карнизе — по линии карниза плана потолков (лист 17); Σ P = Вт/м × длина. Блок питания загружен не больше чем на 80 %; лента 24 В длиннее 10 м питается с двух концов; доступ к блоку питания — люк ревизии 300×300 мм или место, указанное в таблице.
4. Сценарии: уровень — доля максимальной яркости группы, %; 0 — группа выключена. Уровень ниже 100 % — только у групп на светорегуляторе (задний фронт, ТЕ) с диммируемыми драйверами и блоками питания.
5. Мощность и поток — по паспортам принятых изделий, Σ P — установленная мощность освещения. Оценка освещённости — на плане освещения; это не светотехнический расчёт.

					Проект: Квартира 65 м²
	Лист	№ док.	Подпись	Дата	Спецификация светильников и сценарии освещения
Дизайнер	Кырлан А.С.			21.10.26	Стадия: П; Лист: 21; Листов: 80

выпуск 09.10.2026 № da691793fd · стр. 21 из 80

Правка к этому листу

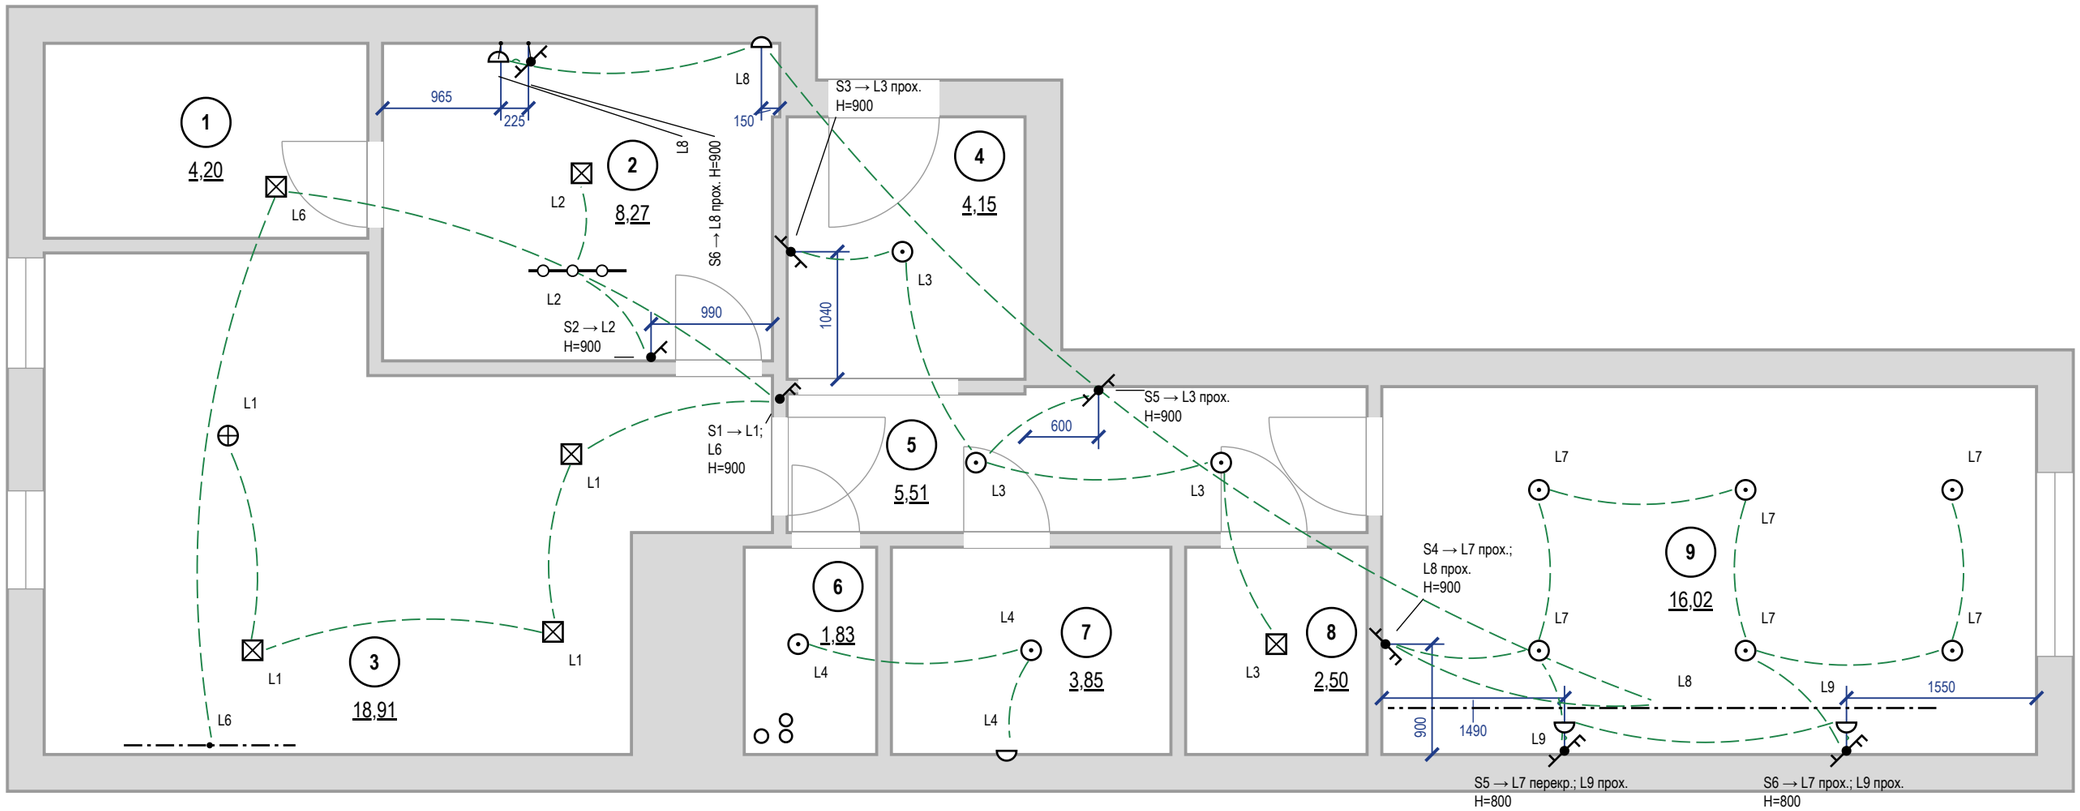

Примечания

1. За отметку 0,000 принят уровень чистого пола. Высоты H — от чистого пола до оси изделия; привязки — от чистовой грани стены до оси механизма (у рамки на несколько постов — до оси рамки).
2. Высота установки, не указанная на плане: выключатели — 900 мм от чистого пола, со стороны дверной ручки (ПУЭ 7.1.51).
3. Линии связи показывают, какой выключатель какую группу L включает; это не трасса кабеля. Трасса — принципиальная, фактическую зафиксировать исполнительной схемой.
4. Группы из нескольких мест (L8 — S4, S6; L3 — S3, S5; L7 — S4, S5, S6; L9 — S5, S6): на крайних местах — проходные клавиши, на промежуточных — перекрёстные; механизмы — в ведомости изделий.
5. Вентиляторы санузлов (выводы ЭВ на плане розеток) включаются вместе с основным светом помещения, отключаются с задержкой — таймер выбега в вентиляторе.
6. Розеточные и мокрые линии — через УЗО или дифавтомат с током утечки не более 30 мА (ПУЭ 7.1.79); в санузле выполнить ДСУП (ПУЭ 7.1.87–7.1.88).
7. Кабель — медный, исполнение нг(A)-LS (ГОСТ 31565-2012); скрытая прокладка только горизонтально и вертикально, фактические трассы зафиксировать исполнительной схемой до закрытия отделкой.
8. Расчёт нагрузок, токов КЗ, селективности и сечений — по проекту ЭОМ организации с допуском СРО; лист задаёт состав, расположение и группы.
9. Группы без выключателя: L4 — назначить управление до монтажа.
10. Расшифровка клавиш и ведомость изделий — лист «Ведомость электроточек и изделий».

					Проект: Квартира 65 м²
	Лист	№ док.	Подпись	Дата	Управление светильниками
Дизайнер	Кырлан А.С.			21.10.26	

Стадия	Лист	Листов
П	22	80

выпуск 09.10.2026 № da691793fd · стр. 22 из 80

Правка к этому листу



Примечания

1. Расчёт систем ОВ и подбор оборудования — проектная организация с допуском СРО; лист даёт места, трассы и привязки.
2. Нормы вытяжки — СП 54.13330.2022 (Изм. 1, 2), табл. 7.1: кухня с электроплитой 60 м³/ч, с газовой 100; ванная и совмещённый санузел 50; уборная 25; гардеробная 0,2 ч⁻¹. Приток в жилые — 3 м³/ч на 1 м² (менее 20 м² общей площади на человека), иначе 30 м³/ч на человека.
3. Вентканалы и шахты не сужать, не переносить и не закрывать; вентилятор и кухонная вытяжка — через обратный клапан, без перекрытия естественной тяги.
4. Проектные расходы — не ниже нормы, вытяжка сведена с притоком вентиляторами мокрых помещений. Клапаны — в простенке у окна, центр 2000 мм, не над кроватью, не ближе 300 мм к стоякам отопления; типоразмер — на расход.
5. Кухонная вытяжка в воздухообмен не включена: воздуховод не менее Ø125 в коробе, вход в канал отдельный.
6. Переток — зазор под полотнами межкомнатных дверей или переточная решётка.
7. Кондиционирование заданием не предусмотрено; при установке трассы фреона и дренажа (не менее 40 мм/м, в К1 через сифон) и питание заложить до черновых работ.
8. Привязки оборудования — по паспортам приобретённых моделей, до черновых работ.

					Проект: Квартира 65 м²
	Лист	№ док.	Подпись	Дата	План вентиляции
Дизайнер	Кырлан А.С.			21.10.26	

Стадия	Лист	Листов
П	23	80

Правка к этому листу



Примечания

1. Расчёт системы отопления, теплопотерь и подбор приборов — проектная организация с допуском СРО; лист даёт места и привязки.
2. Тип, длина и мощность радиаторов — по теплотехническому расчёту; лист задаёт места, зазоры и подключение.
3. Зазоры радиатора: низ не менее 100 мм от чистого пола, верх не менее 100 мм до подоконника, 30–50 мм от стены до задней панели; центр по оси окна с допуском ±20 мм.
4. Радиаторы не закрывать глухими коробами и мебелью; перенос и замена приборов в многоквартирном доме — переустройство, согласование с управляющей организацией (ЖК РФ ст. 25–26); вынос на лоджию запрещён.
5. Трубы отопления через межквартирные стены не прокладывать (СП 51.13330.2011, п. 9.19); через перекрытия и перегородки — в гильзах.
6. Привязки приборов и подводок — по паспортам приобретённых радиаторов и клапанов, до черновых работ.
7. До закрытия отделкой трубопроводы отопления испытать гидростатическим давлением с оформлением акта (СП 73.13330.2016, 7.2–7.3).

					Проект: Квартира 65 м²			
	Лист	№ док.	Подпись	Дата				
Дизайнер	Кырлан А.С.			21.10.26	План отопления	Стадия	Лист	Листов
						П	24	80


выпуск 09.10.2026 № da691793fd · стр. 24 из 80

Правка к этому листу

Спецификация плинтусов


Наименование	Помещения	Длина, м (с запасом)
SX165, h = 69 мм, крепление к стене, окраска в цвет Tikkurila V503	1, 2, 3, 4, 5, 8, 9	79

Экспликация полов

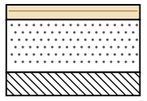Номер помещения	Тип пола	Схема пола	Данные элементов пола (наименование, толщина, основание), мм	Площадь, м²
1, 9	1		Инженерная доска на клею — 14 Стяжка ЦПС М200 — 50 Плита перекрытия Всего 64 мм; ЧП ±0,000, верх плиты −0,064	20,22
2, 3, 8	2		Инженерная доска, IM1848, 1380×190 мм, на клею ЧП ±0,000	29,68
4, 5	3		Керамогранит, SG501600R, 600×1200 мм ЧП ±0,000	9,66
6, 7	4		Керамогранит, SG501600R, 600×1200 мм Гидроизоляция обмазочная, 2 слоя, с заведением на стены 200 мм ЧП −0,015	5,68
			Итого	**65,24**

Отметки по высоте

±0,000 чистый пол пом. 1–5, 8, 9; отсчёт высот
−0,015 чистый пол пом. 6, 7, ниже на 15 мм
−0,064 верх плиты — расчёт, не замер (задание на обмер)
сущ. пол снимается до плиты; не замерен (задание на обмер)

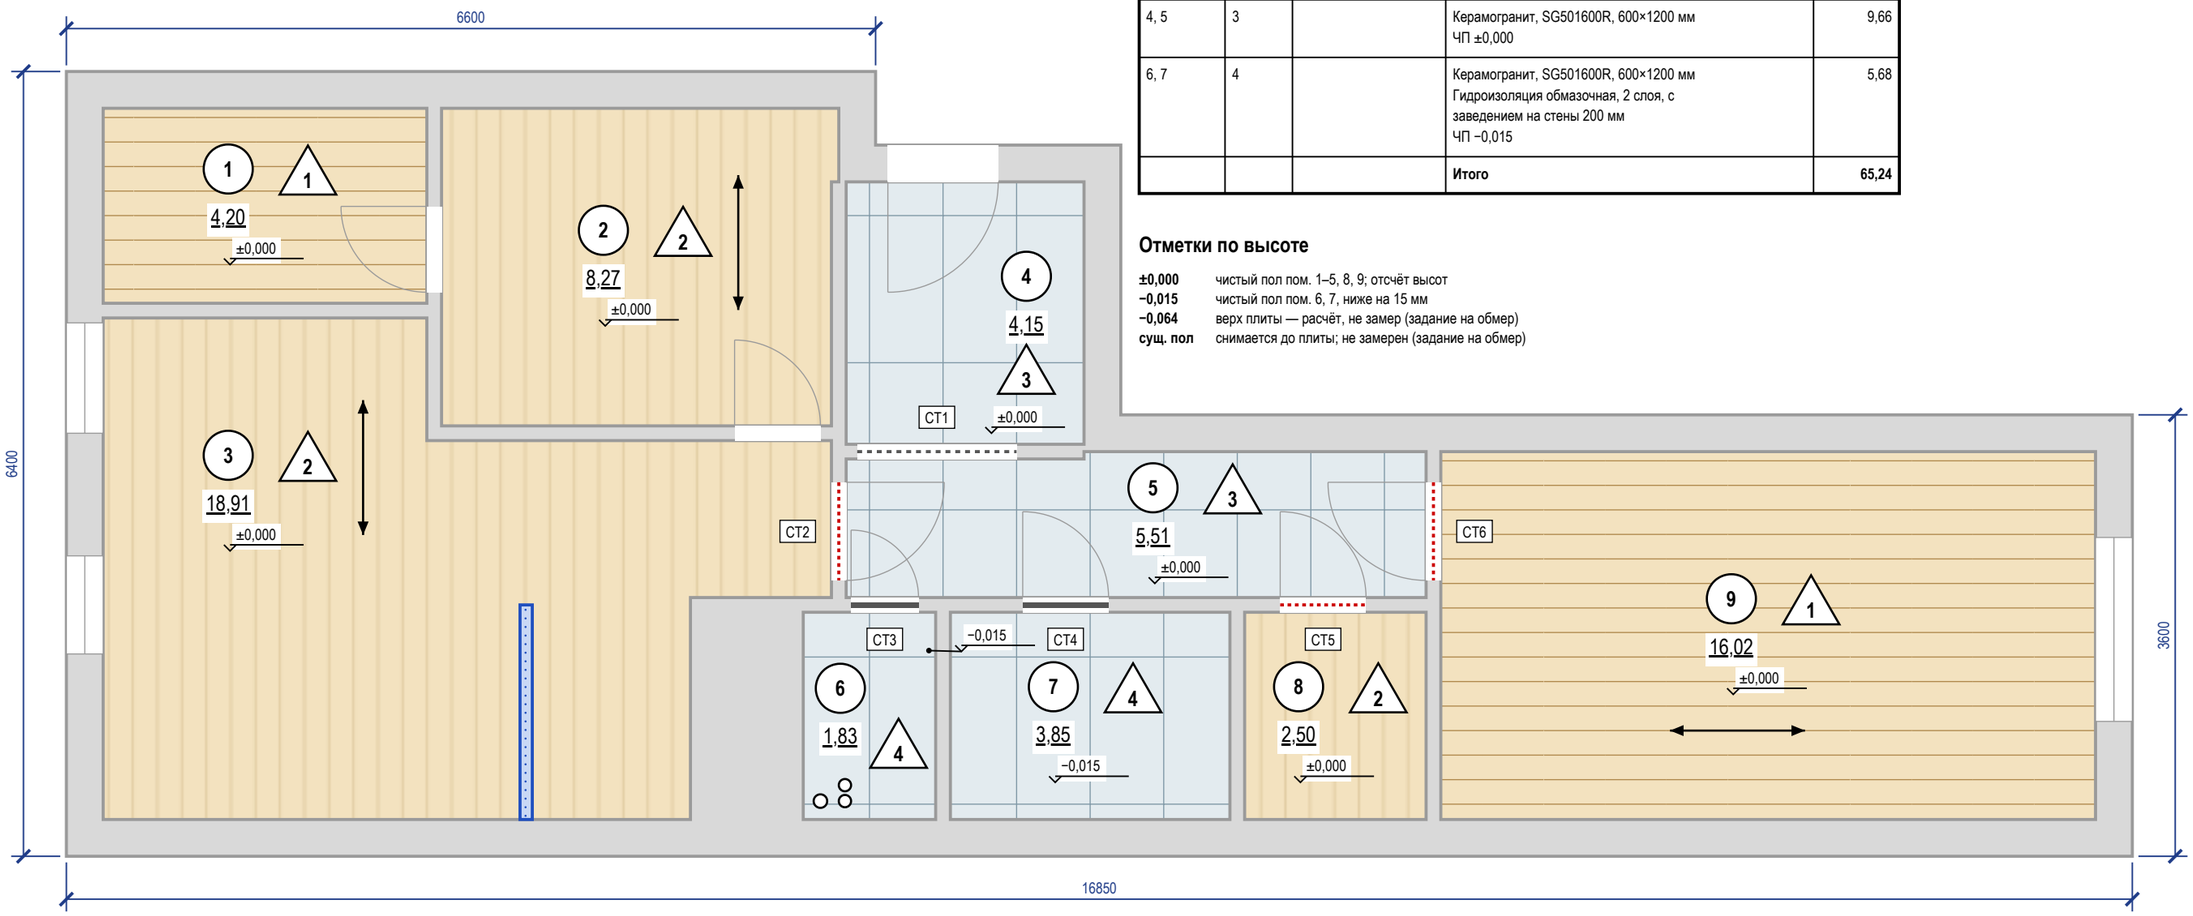

Примечания

1. За отметку ±0,000 принят чистый пол, не существующий (блок отметок). Площади — по чистым размерам помещений, м²; размеры — в мм.
2. Стык разнотипных покрытий — по оси дверного полотна (под полотном в закрытом положении); решение стыка — по ведомости стыков.
3. Пол санузлов ниже смежных помещений на 15 мм за счёт меньшей толщины стяжки (верх плиты общий — по экспликации полов); гидроизоляция по стяжке с заведением на стены не менее 200 мм (СП 29.13330.2011, п. 7.2), до облицовки — тест проливом и акт скрытых работ.
4. Выпуски канализации с уклоном и трассы водоснабжения — в слое засыпки под стяжкой (по экспликации полов); отметки, уклоны и прочистки — по листу разводки ВК 14.
5. Звукоизоляционный слой под стяжкой проектом не предусмотрен (стяжка по плите): приведённый уровень ударного шума перекрытия с полом Lnw не более 60 дБ (СП 51.13330.2011, табл. 2) подтвердить по данным дома; при превышении — плавающая стяжка по звукоизоляции с демпферной лентой по контуру и у стояков, пирог пересчитать.
6. Штучные покрытия (инженерная доска): направление — по стрелке; влажность основания по СМ не более 2,0 % (по ТУ изготовителя).
7. Ровность основания — просвет под 2-метровой рейкой не более 2 мм: пом. 1, 2, 3, 8, 9 (инженерная доска), пом. 4, 5, 6, 7 (керамогранит); проверить до укладки покрытия (СП 71.13330.2017, табл. 8.5).
8. Сетка на плитке — условная, в размер формата; точка старта и раскладка — по листу раскладки плитки.
9. Узор покрытия (заливка-код типа пола) прерывается под надписями — площадями помещений и отметками чистого пола.
10. Пироги полов — по экспликации полов: слои сверху вниз, толщины в мм; гидроизоляция мокрых зон — в пироге и в ведомости отделки; схема пола — без масштаба.

					Проект: Квартира 65 м²
	Лист	№ док.	Подпись	Дата	План покрытий пола
Дизайнер	Кырлан А.С.			21.10.26	

Стадия	Лист	Листов
П	25	80

Ведомость плитки

Помещение, поверхность	Плитка, код	Формат	Шов	S, м²	Целых	Подр.	С запасом
Прихожая, пол	SG501600R	600×1200	2	4,15	0	8	9
Коридор, пол	SG501600R	600×1200	2	5,51	0	8	9
Санузел, пол	SG501600R	600×1200	2	1,83	0	4	5
Ванная, пол	SG501600R	600×1200	2	3,85	0	8	9
Итого 600×1200				**15,34**	**0**	**28**	**32**

Ведомость материалов

Материал	Класс, код	Норма расхода	Кол-во
Затирка	класс не задан	(a+b)/ab·шов·t·1,6	1,2 кг
Клей	C2	1,5 кг/м²·мм, слой 5	79 кг (4 меш.)
Клей	C2 S1	1,5 кг/м²·мм, слой 5	46 кг (2 меш.)
Демпф. лента	по периметру пола из плитки		27,2 м

Условные обозначения

- плитка целая; тонкая линия — шов
- плитка с подрезкой (размер — на цепочке)
- ось старта; стрелки — направление укладки
- сантехприбор: габарит, высота по практике
- отметка чистого пола на полке выноски, м
- (А) обозначение стены А–Г (как на развёртках)

Примечания


1. Плитка пола мокрых помещений не задана — планы полов санузлов не выполнены; на листе — ведомость плитки остальных помещений.
2. Толщины облицовки стен не заданы: раскладка от черновых размеров, до укладки пересчитать от чистовых.
3. Раскладка пола «Прихожая» и пола «Коридор» и пола «Санузел» и пола «Ванная» — на листе «Раскладка плитки. Прихожая. Коридор. Санузел. Ванная».
4. Калибр партии не задан — до укладки замерить (рабочий размер W, ГОСТ 13996-2019) и пересчитать подрезки.
5. Количество: целые по раскладке + по одной на подрезку, запас 10 %; один артикул — одна партия и тон. Исключены поддон, короб, проёмы и места за коробом; S — по чистым граням, как в ведомости отделки.
6. Клей C2; C2 S1 (ГОСТ Р 56387-2018), затирка класс не задан; расход — по ТУ выбранной марки.

	Лист	№ док.	Подпись	Дата	Проект: Квартира 65 м²			
Дизайнер	Кырлан А.С.			21.10.26	Раскладка плитки. Планы полов	Стадия	Лист	Листов
						П	26	80


выпуск 09.10.2026 № da691793fd · стр. 26 из 80

Правка к этому листу


Фрагмент 1. Прихожая (пом. 4). Пол 600×1200, шов 2 мм, М 1:40

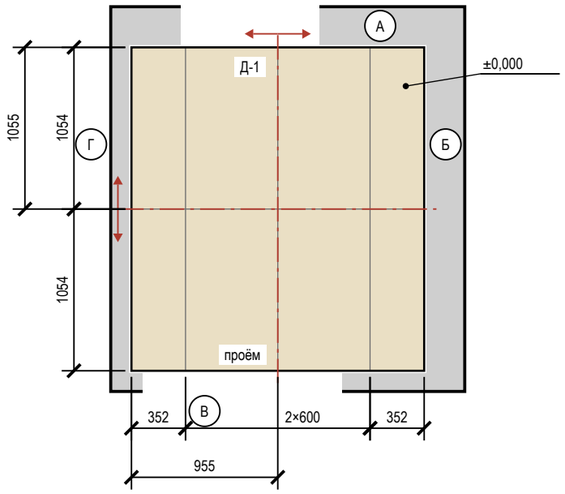


Фрагмент 2. Коридор (пом. 5). Пол 600×1200, шов 2 мм, М 1:40

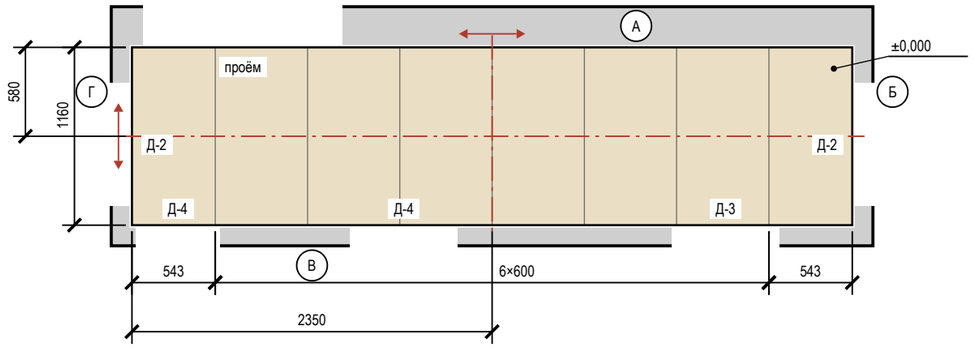

Фрагмент 3. Санузел (пом. 6). Пол 600×1200, шов 2 мм, М 1:40

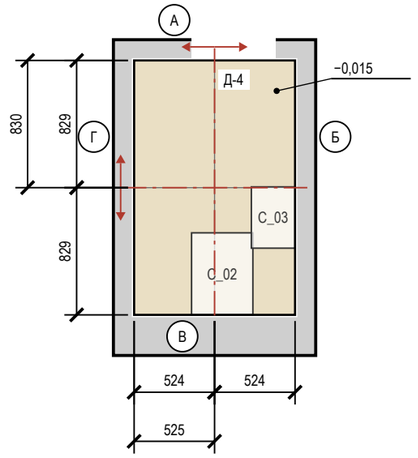

Фрагмент 4. Ванная (пом. 7). Пол 600×1200, шов 2 мм, М 1:40

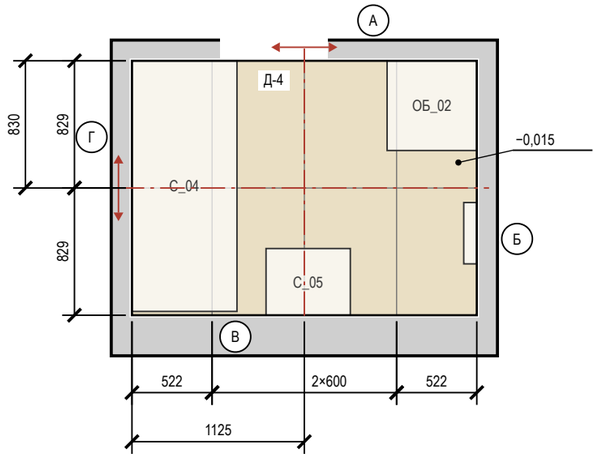

Условные обозначения

- плитка целая; тонкая линия — шов
- плитка с подрезкой (размер — на цепочке)
- ось старта; стрелки — направление укладки
- отметка чистого пола на полке выноски, м
- (А) обозначение стены А–Г (как на развёртках)

Подсчёт плитки

Поверхность	Формат	S, м²	Целых	Подр.	С запасом
Прихожая, пол	600×1200	4,15	0	8	9
Коридор, пол	600×1200	5,51	0	8	9
Санузел, пол	600×1200	1,83	0	4	5
Ванная, пол	600×1200	3,85	0	8	9

Примечания

1. Прихожая: керамогранит 600×1200, длинная сторона — вдоль стен Б и Г, шов 2 мм, прямая раскладка от центра. Стены окрашены: раскладка от чистового контура минус штукатурка и шпаклёвка 15 мм на сторону (принято); подрезки 352 / 1054 мм, срез — под плинтус.
2. Прихожая: деформационный зазор по периметру 8–10 мм под плинтусом; в проёмах — стык с соседним покрытием по оси полотна двери. Клей С2, затирка класс не задан.
3. Коридор: керамогранит 600×1200, длинная сторона — вдоль стен Б и Г, шов 2 мм, прямая раскладка от центра. Стены окрашены: раскладка от чистового контура минус штукатурка и шпаклёвка 15 мм на сторону (принято); подрезки 543 / 1160 мм, срез — под плинтус.
4. Коридор: деформационный зазор по периметру 8–10 мм под плинтусом; в проёмах — стык с соседним покрытием по оси полотна двери. Клей С2, затирка класс не задан.
5. Санузел: керамогранит 600×1200, длинная сторона — вдоль стен Б и Г, шов 2 мм, прямая раскладка от центра. Стены окрашены: раскладка от чистового контура минус штукатурка и шпаклёвка 15 мм на сторону (принято); подрезки 524 / 829 мм, срез — под плинтус.
6. Санузел: деформационный зазор по периметру 8–10 мм под плинтусом; в проёмах — стык с соседним покрытием по оси полотна двери. Клей С2 S1, затирка класс не задан.
7. Ванная: керамогранит 600×1200, длинная сторона — вдоль стен Б и Г, шов 2 мм, прямая раскладка от центра. Стены окрашены: раскладка от чистового контура минус штукатурка и шпаклёвка 15 мм на сторону (принято); подрезки 522 / 829 мм, срез — под плинтус.
8. Ванная: деформационный зазор по периметру 8–10 мм под плинтусом; в проёмах — стык с соседним покрытием по оси полотна двери. Клей С2 S1, затирка класс не задан.
9. Клей, затирка и итог по форматам — в ведомостях листа «Раскладка плитки. Планы полов».

					Проект: Квартира 65 м²
	Лист	№ док.	Подпись	Дата	Раскладка плитки. Прихожая. Коридор. Санузел. Ванная
Дизайнер	Кырлан А.С.			21.10.26	

Стадия	Лист	Листов
П	27	80

Правка к этому листу



					Проект: Квартира 65 м²
	Лист	№ док.	Подпись	Дата	
Дизайнер	Кырлан А.С.			21.10.26	Визуализация. Вид сверху

Стадия	Лист	Листов
П	28	80

выпуск 09.10.2026 № da691793fd · стр. 28 из 80

Правка к этому листу




					Проект: Квартира 65 м²
	Лист	№ док.	Подпись	Дата	
Дизайнер	Кырлан А.С.			21.10.26	Визуализация гардеробной
					Стадия: П; Лист: 29; Листов: 80

выпуск 09.10.2026 № da691793fd · стр. 29 из 80

Правка к этому листу

Развёртка стены А

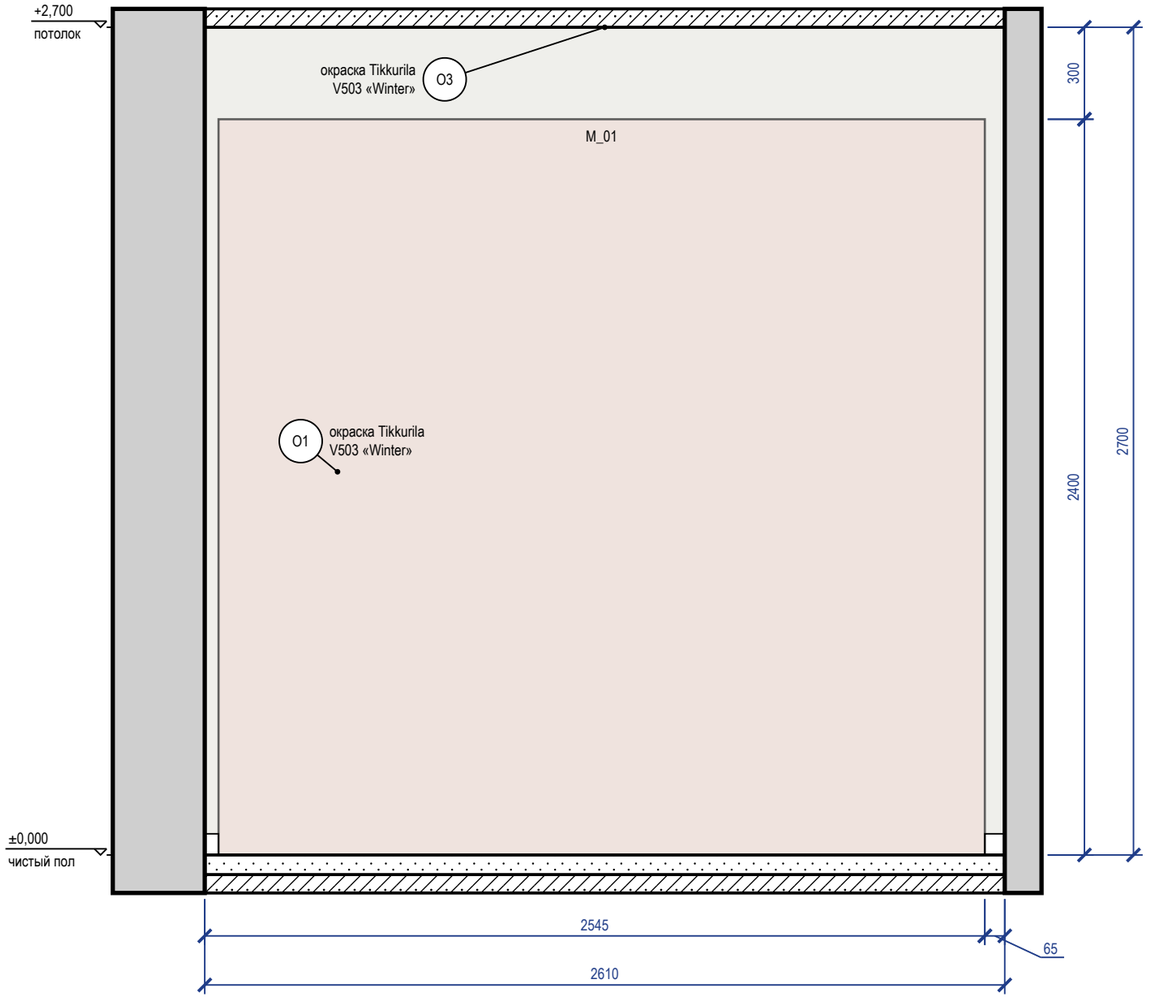

Развёртка стены Б


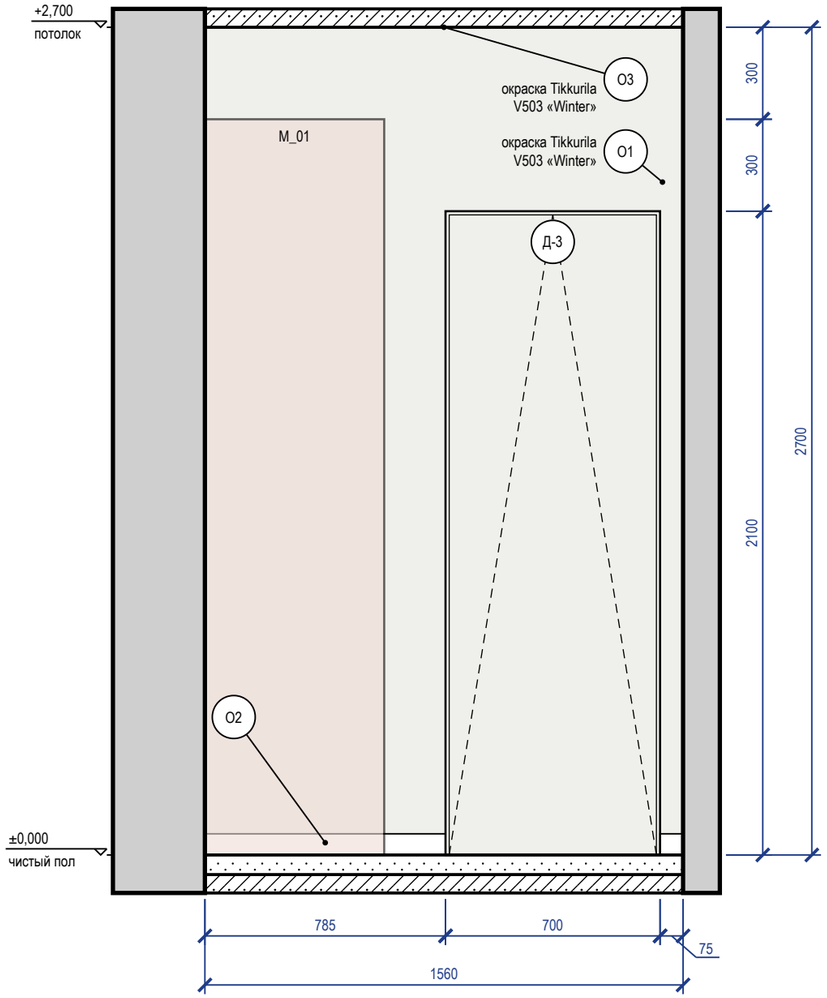


Схема развёрток (М 1:100)

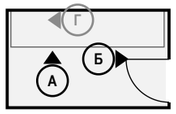

Ведомость отделки (на листе)

Марка	Поверхность	Материал, изделие	Цвет, код	Кол.
О1	стены	окраска, Tikkurila Harmony, матовая, подготовка Q3	Tikkurila V503 «Winter»	9,8 м²
О2	плинтус	плинтус МДФ, Orac Decor Contour (Luxxus), h 69 мм, SX165	Tikkurila V503 «Winter»	1 м
О3	потолок	окраска, Tikkurila Anti-Reflex 2, глубокоматовая, подготовка Q3	Tikkurila V503 «Winter»	4,2 м²

Примечания

1. Размеры — в мм от чистовых поверхностей стен; условные обозначения и общие указания — лист 2.
2. Двери скрытого монтажа — полотно в плоскости стены, отделка стены по полотну, плинтус прерывается у короба (узел — на листе узлов).

					Проект: Квартира 65 м²
	Лист	№ док.	Подпись	Дата	Развёртки стен А, Б. Гардеробная (пом. 1)
Дизайнер	Кырлан А.С.			21.10.26	

Стадия	Лист	Листов
П	30	80

Развёртка стены Г


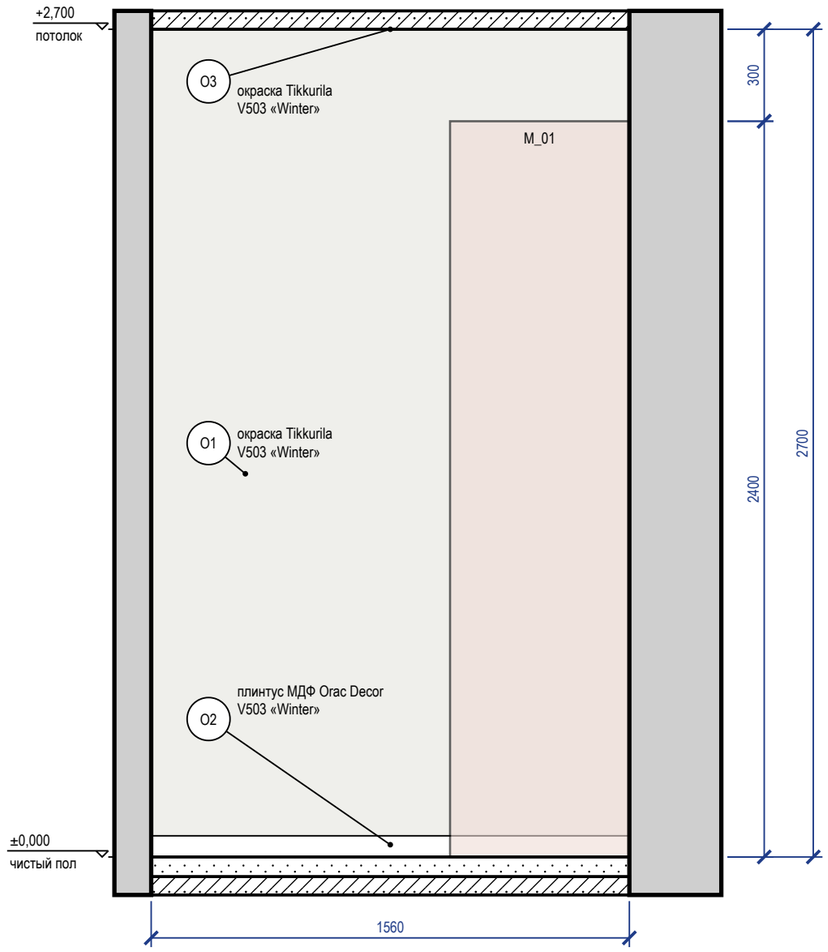


Схема развёрток (М 1:100)

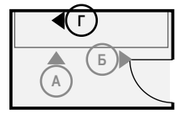

Ведомость отделки (на листе)

Марка	Поверхность	Материал, изделие	Цвет, код	Кол.
О1	стены	окраска, Tikkurila Harmony, матовая, подготовка Q3	Tikkurila V503 «Winter»	4,2 м²
О2	плинтус	плинтус МДФ, Orac Decor Contour (Luxxus), h 69 мм, SX165	Tikkurila V503 «Winter»	1,6 м
О3	потолок	окраска, Tikkurila Anti-Reflex 2, глубокоматовая, подготовка Q3	Tikkurila V503 «Winter»	4,2 м²

Визуализация этой стены — лист 29



Примечания

1. Размеры — в мм от чистовых поверхностей стен; условные обозначения и общие указания — лист 2.

					Проект: Квартира 65 м²		
	Лист	№ док.	Подпись	Дата	Развёртка стены Г. Гардеробная (пом. 1)	Стадия	Лист	Листов
Дизайнер	Кырлан А.С.			21.10.26		П	31	80

Правка к этому листу



					Проект: Квартира 65 м²	
	Лист	№ док.	Подпись	Дата	Визуализация спальни	Стадия / Лист / Листов
Дизайнер	Кырлан А.С.			21.10.26		П / 32 / 80

выпуск 09.10.2026 № da691793fd · стр. 32 из 80

Правка к этому листу



					Проект: Квартира 65 м²	
	Лист	№ док.	Подпись	Дата	Визуализация спальни	Стадия / Лист / Листов
Дизайнер	Кырлан А.С.			21.10.26		П / 33 / 80

выпуск 09.10.2026 № da691793fd · стр. 33 из 80

Развёртка стены А


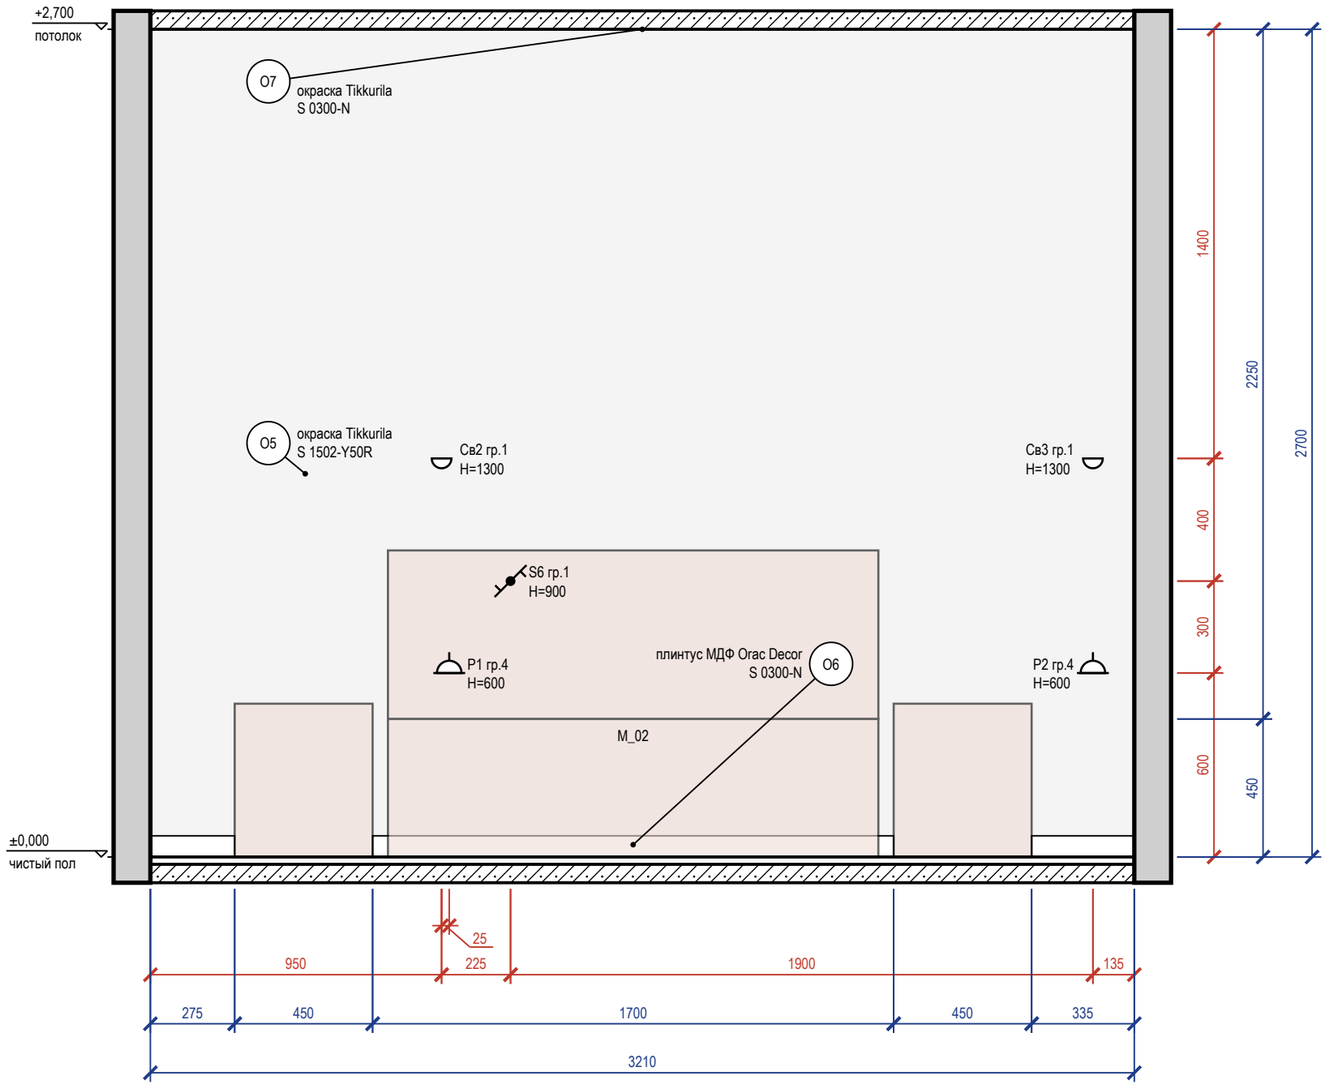


Схема развёрток (М 1:100)

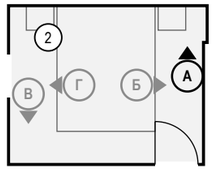

Ведомость отделки (на листе)

Марка	Поверхность	Материал, изделие	Цвет, код	Кол.
О5	стены	окраска, Tikkurila, глубокоматовая, подготовка Q3	NCS S 1502-Y50R	8,7 м²
О6	плинтус	плинтус МДФ, Orac Decor Contour (Luxxus), h 69 мм, SX165, шелковисто-матовая	NCS S 0300-N	2,3 м
О7	потолок	окраска, Tikkurila, глубокоматовая	NCS S 0300-N	8,3 м²

Визуализация этой стены — лист 32



Примечания

1. Размеры — в мм от чистовых поверхностей стен; условные обозначения и общие указания — лист 2.

					Проект: Квартира 65 м²
	Лист	№ док.	Подпись	Дата	Развёртка стены А. Спальня (пом. 2)
Дизайнер	Кырлан А.С.			21.10.26	

Стадия	Лист	Листов
П	34	80

Правка к этому листу

Развёртка стены Б


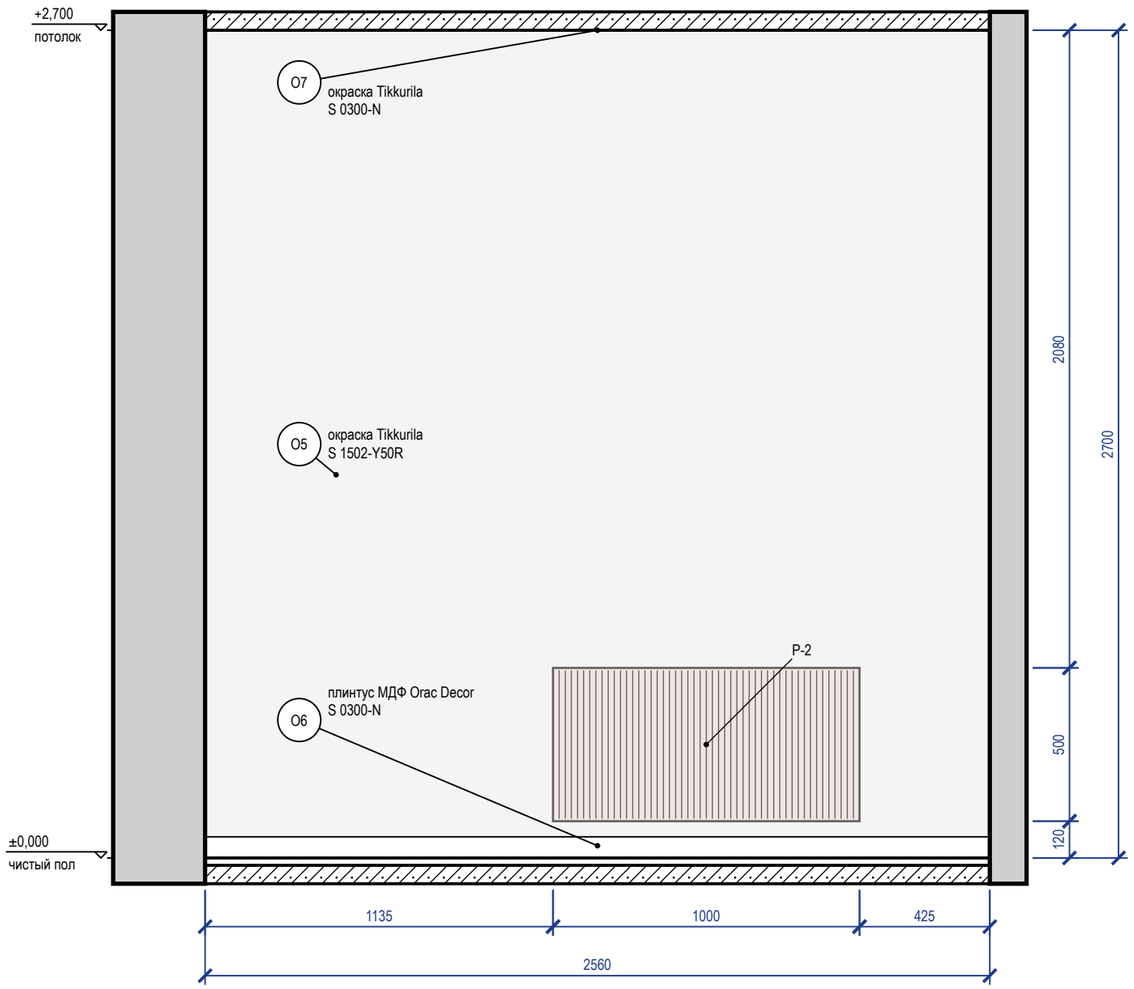


Схема развёрток (М 1:100)

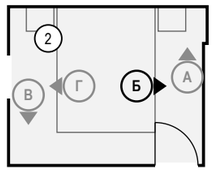

Ведомость отделки (на листе)

Марка	Поверхность	Материал, изделие	Цвет, код	Кол.
О5	стены	окраска, Tikkurila, глубокоматовая, подготовка Q3	NCS S 1502-Y50R	6,9 м²
О6	плинтус	плинтус МДФ, Orac Decor Contour (Luxxus), h 69 мм, SX165, шелковисто-матовая	NCS S 0300-N	2,6 м
О7	потолок	окраска, Tikkurila, глубокоматовая	NCS S 0300-N	8,3 м²

Примечания

1. Размеры — в мм от чистовых поверхностей стен; условные обозначения и общие указания — лист 2.

					Проект: Квартира 65 м²
	Лист	№ док.	Подпись	Дата	Развёртка стены Б. Спальня (пом. 2)
Дизайнер	Кырлан А.С.			21.10.26	

Стадия	Лист	Листов
П	35	80

выпуск 09.10.2026 № da691793fd · стр. 35 из 80

Правка к этому листу

Развёртка стены В


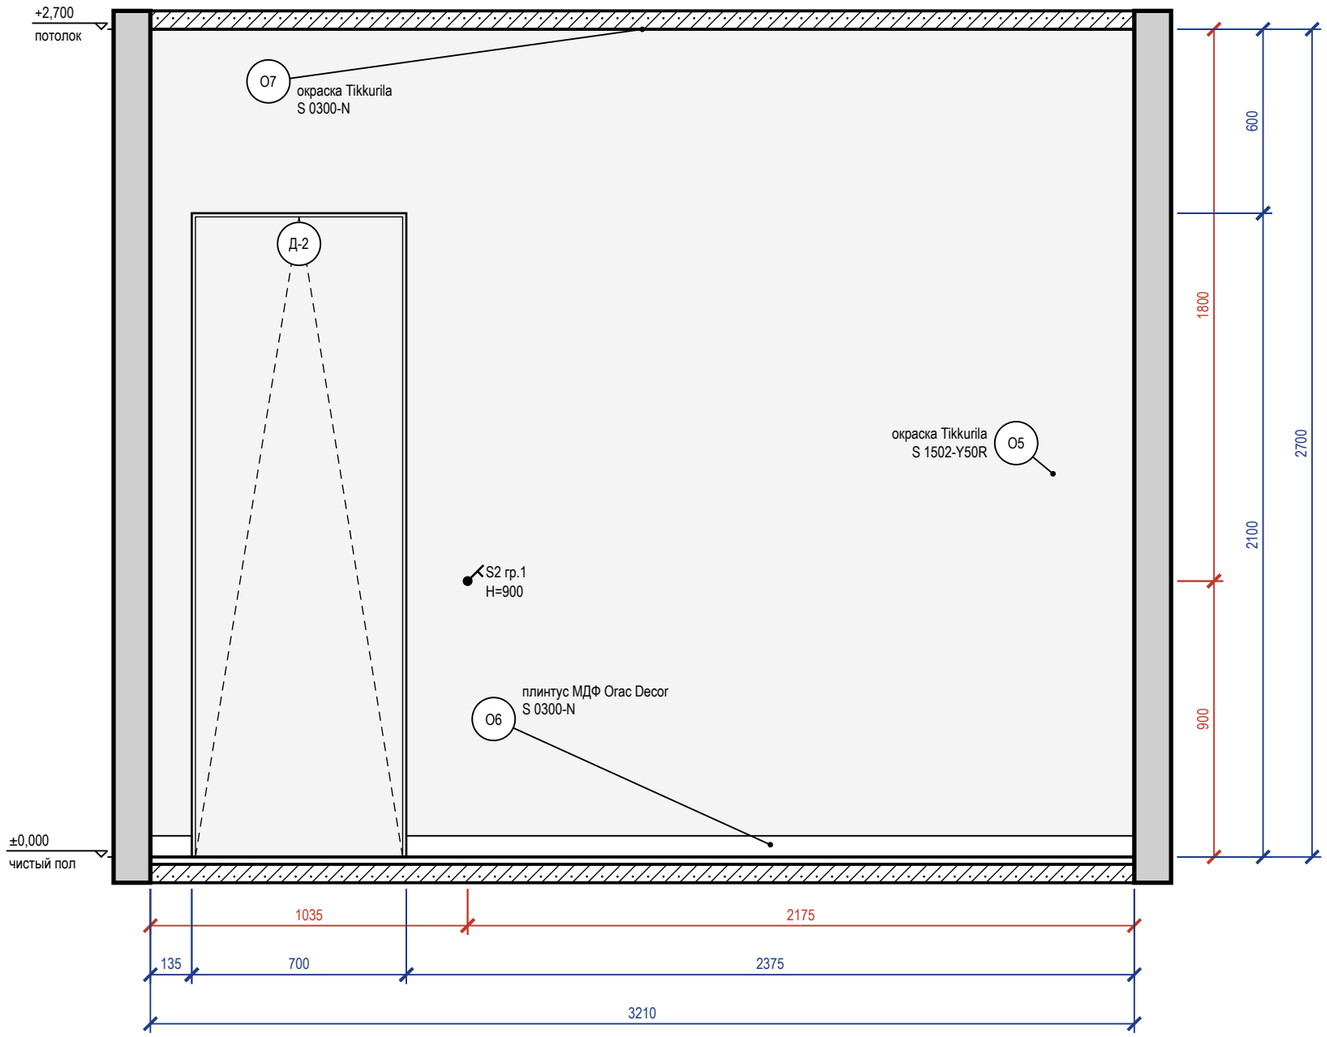



Схема развёрток (М 1:100)

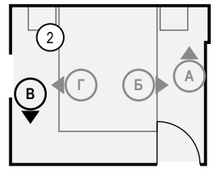

Ведомость отделки (на листе)

Марка	Поверхность	Материал, изделие	Цвет, код	Кол.
О5	стены	окраска, Tikkurila, глубокоматовая, подготовка Q3	NCS S 1502-Y50R	7,2 м²
О6	плинтус	плинтус МДФ, Orac Decor Contour (Luxxus), h 69 мм, SX165, шелковисто-матовая	NCS S 0300-N	2,5 м
О7	потолок	окраска, Tikkurila, глубокоматовая	NCS S 0300-N	8,3 м²

5 **Плинтус МДФ 69×16 мм у окрашенной стены (М 1:10)**
Узел 5 — лист С3

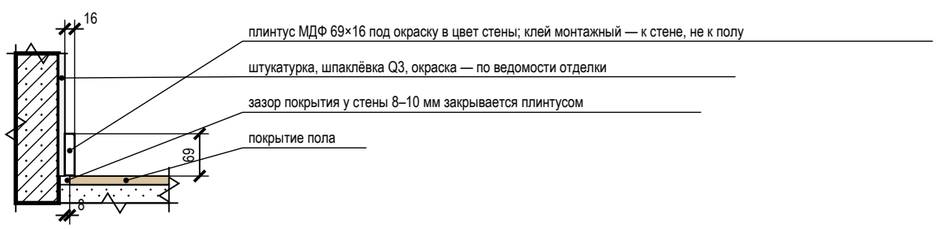

Примечания

1. Размеры — в мм от чистовых поверхностей стен; условные обозначения и общие указания — лист 2.
2. Двери скрытого монтажа — полотно в плоскости стены, отделка стены по полотну, плинтус прерывается у короба (узел — на листе узлов).

					Проект: Квартира 65 м²
	Лист	№ док.	Подпись	Дата	Развёртка стены В. Спальня (пом. 2)
Дизайнер	Кырлан А.С.			21.10.26	

Стадия	Лист	Листов
П	36	80

выпуск 09.10.2026 № da691793fd · стр. 36 из 80

Правка к этому листу

Развёртка стены Г


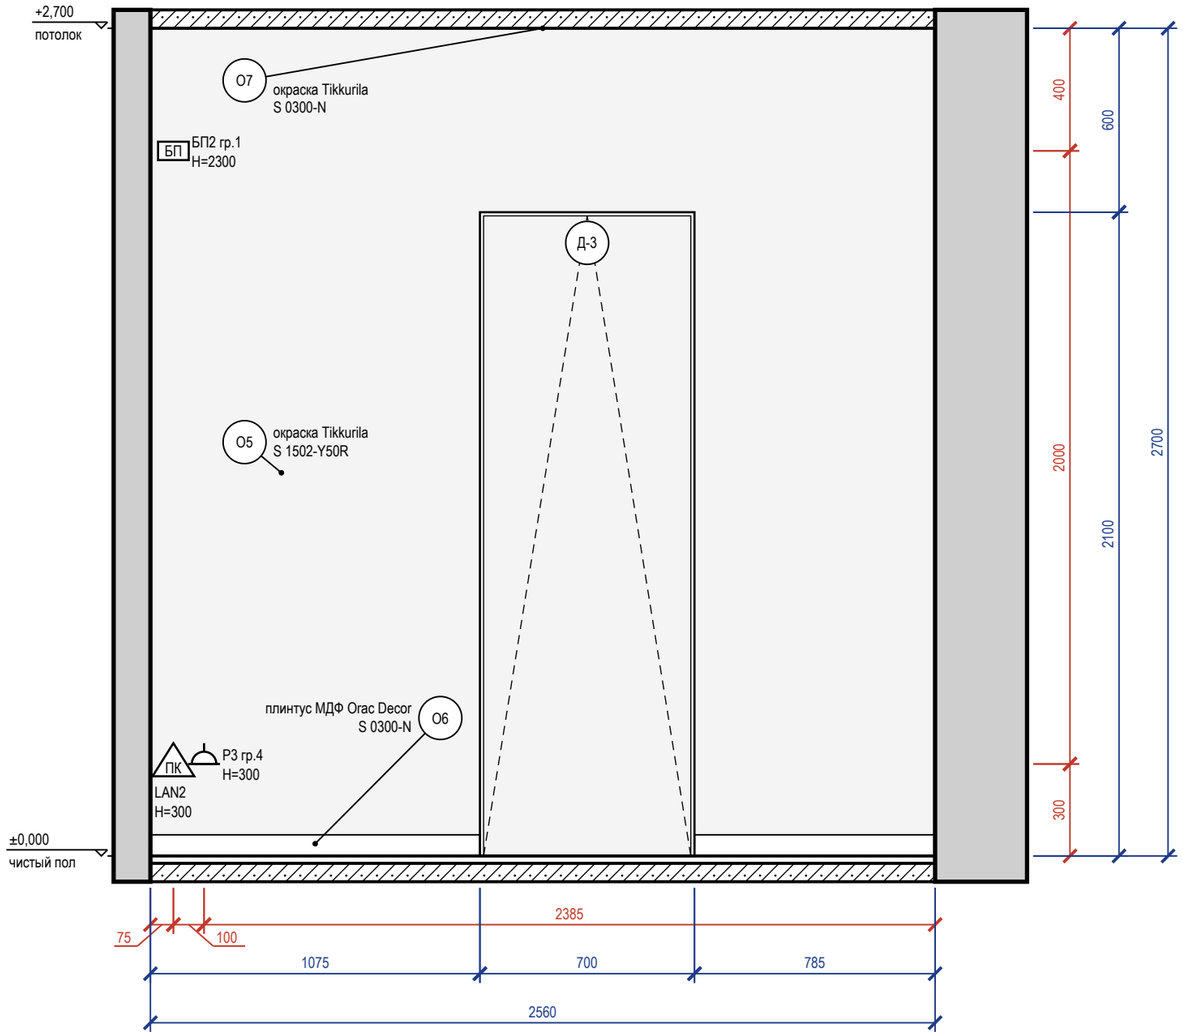


Схема развёрток (М 1:100)

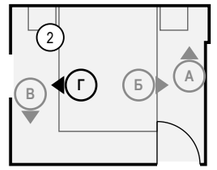

Ведомость отделки (на листе)


Марка	Поверхность	Материал, изделие	Цвет, код	Кол.
О5	стены	окраска, Tikkurila, глубокоматовая, подготовка Q3	NCS S 1502-Y50R	5,4 м²
О6	плинтус	плинтус МДФ, Orac Decor Contour (Luxxus), h 69 мм, SX165, шелковисто-матовая	NCS S 0300-N	1,9 м
О7	потолок	окраска, Tikkurila, глубокоматовая	NCS S 0300-N	8,3 м²

Визуализация этой стены — лист 33



2 **Дверь скрытого монтажа в плоскости стены, плинтус (М 1:10)**

Узел 2 — лист С3

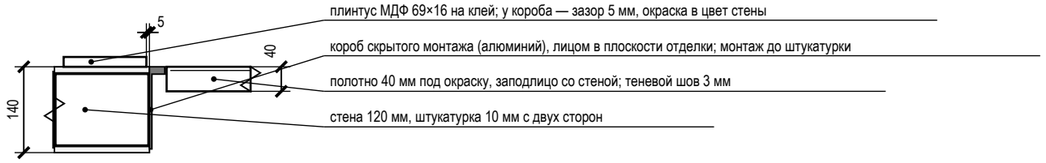

Примечания

1. Размеры — в мм от чистовых поверхностей стен; условные обозначения и общие указания — лист 2.
2. Двери скрытого монтажа — полотно в плоскости стены, отделка стены по полотну, плинтус прерывается у короба (узел — на листе узлов).

					Проект: Квартира 65 м²			
	Лист	№ док.	Подпись	Дата	Развёртка стены Г. Спальня (пом. 2)	Стадия	Лист	Листов
Дизайнер	Кырлан А.С.			21.10.26		П	37	80

Правка к этому листу



					Проект: Квартира 65 м²	
	Лист	№ док.	Подпись	Дата	Визуализация кухни-гостиной	Стадия / Лист / Листов
Дизайнер	Кырлан А.С.			21.10.26		П / 38 / 80

выпуск 09.10.2026 · da691793fd · стр. 38 из 80

Правка к этому листу



					Проект: Квартира 65 м²	
	Лист	№ док.	Подпись	Дата	Визуализация кухни-гостиной	Стадия / Лист / Листов
Дизайнер	Кырлан А.С.			21.10.26		П / 39 / 80

выпуск 09.10.2026 № da691793fd · стр. 39 из 80

Правка к этому листу



					Проект: Квартира 65 м²	
	Лист	№ док.	Подпись	Дата	Визуализация кухни-гостиной	Стадия / Лист / Листов
Дизайнер	Кырлан А.С.			21.10.26		П / 40 / 80

выпуск 09.10.2026 № da691793fd · стр. 40 из 80

Правка к этому листу



					Проект: Квартира 65 м²	
	Лист	№ док.	Подпись	Дата		
Дизайнер	Кырлан А.С.			21.10.26	Визуализация кухни-гостиной	Стадия / Лист / Листов
						П / 41 / 80

выпуск 09.10.2026 · da691793fd · стр. 41 из 80

Правка к этому листу

Развёртка стены В2


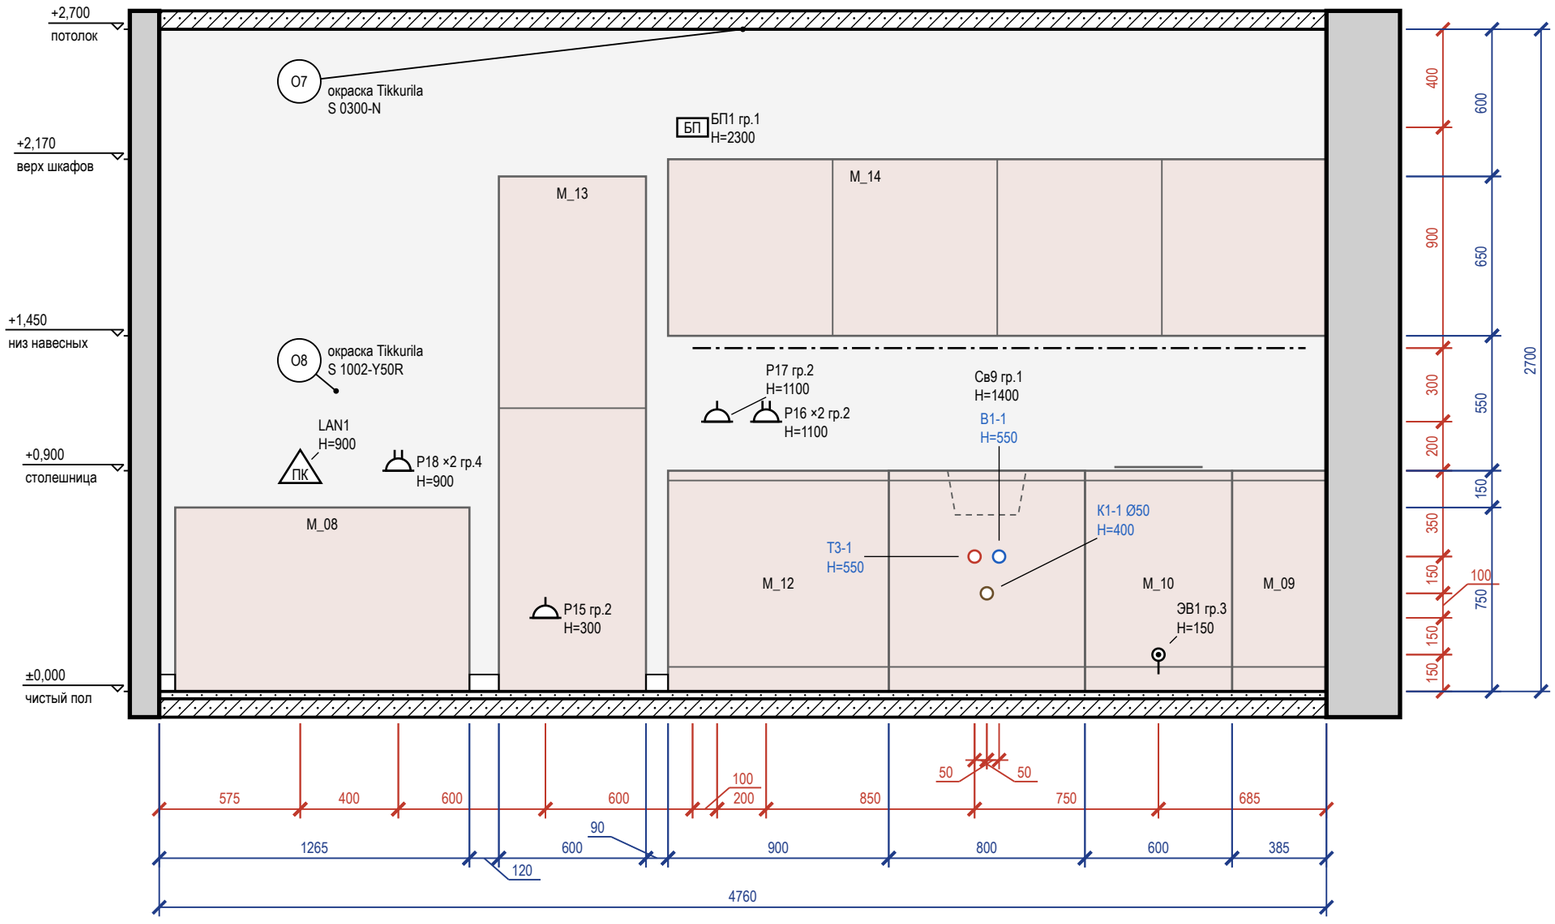


Схема развёрток (М 1:100)

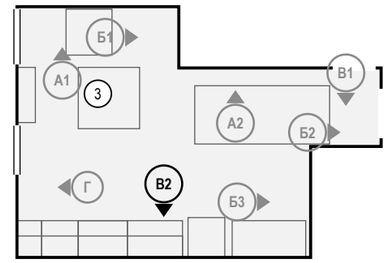

Ведомость отделки (на листе)

Марка	Поверхность	Материал, изделие	Цвет, код	Кол.
О6	плинтус	плинтус МДФ, Orac Decor Contour (Luxxus), h 69 мм, SX165, шелковисто-матовая	NCS S 0300-N	0,3 м
О7	потолок	окраска, Tikkurila, глубокоматовая	NCS S 0300-N	18,9 м²
О8	стены	окраска, Tikkurila, шелковисто-матовая, подготовка Q3	NCS S 1002-Y50R	12,9 м²

Визуализация этой стены — лист 38



Примечания

1. Размеры — в мм от чистовых поверхностей стен; условные обозначения и общие указания — лист 2.
2. Выводы кухонной техники — по утверждённому проекту кухни: привязки выводов даются от осей модулей гарнитура.


					Проект: Квартира 65 м²
	Лист	№ док.	Подпись	Дата	Развёртка стены В2. Кухня-гостиная (пом. 3), кухонный
Дизайнер	Кырлан А.С.			21.10.26	

Стадия	Лист	Листов
П	42	80

выпуск 09.10.2026 № da691793fd · стр. 42 из 80

Правка к этому листу


Развёртка стены Г

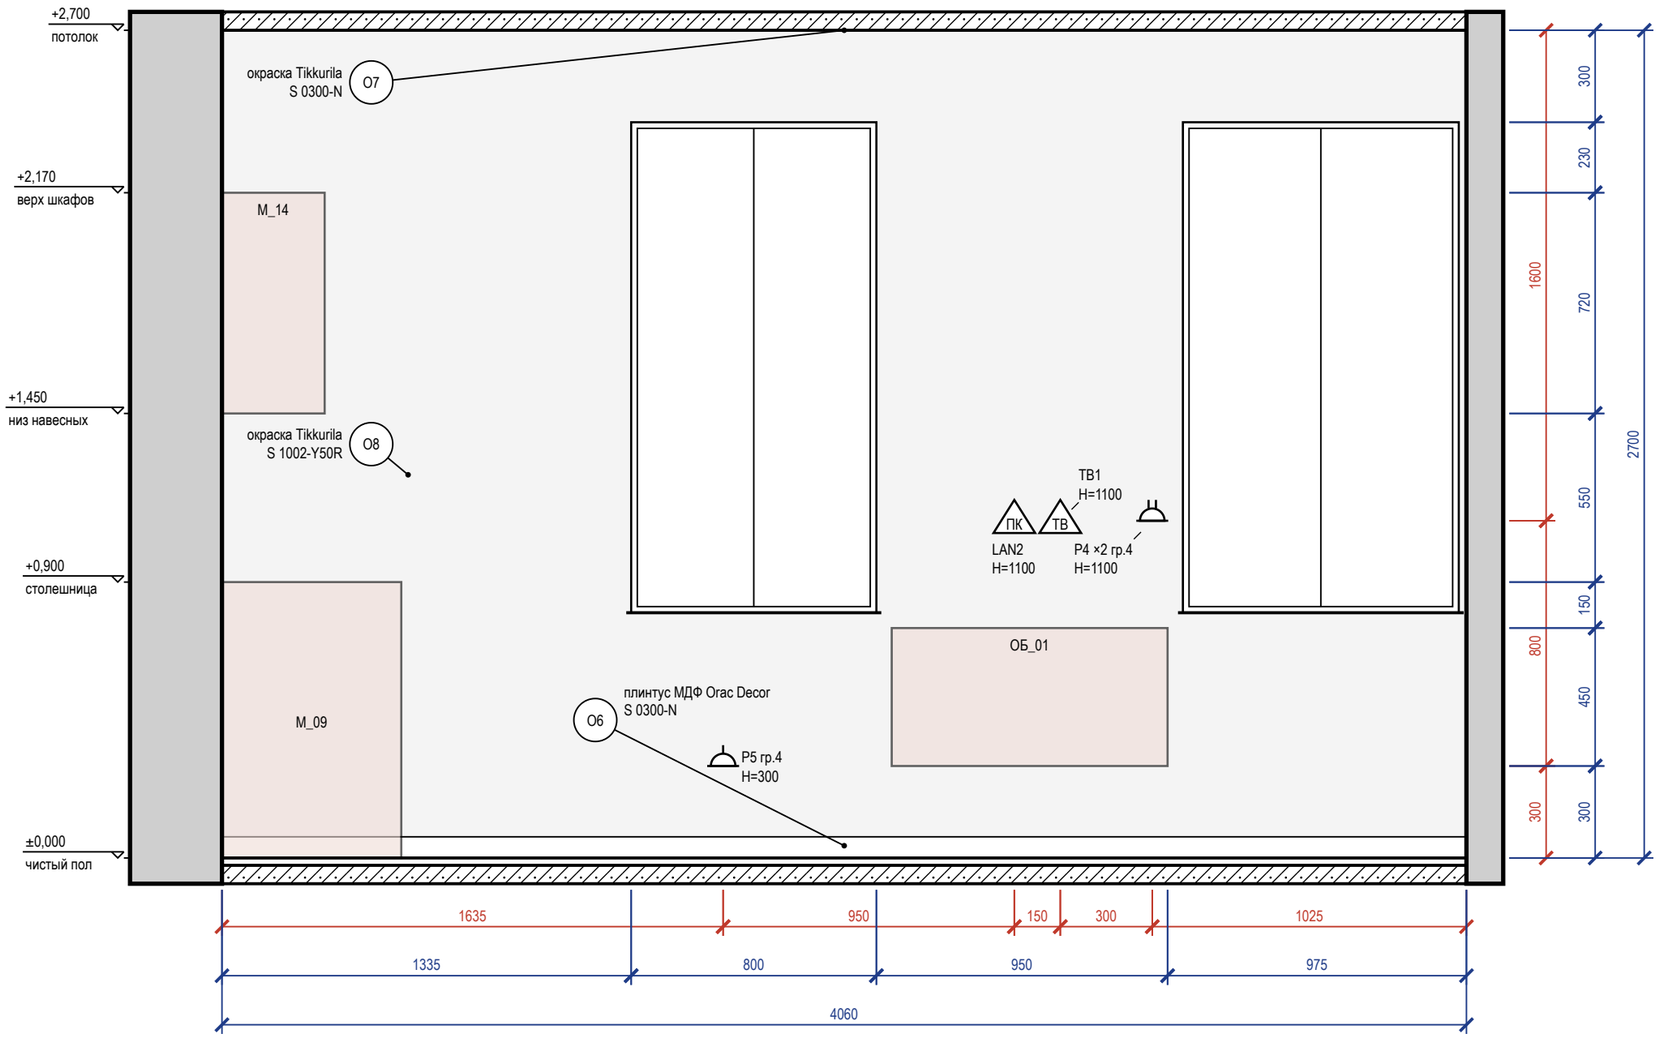

Визуализация этой стены — лист 39



Схема развёрток (М 1:100)

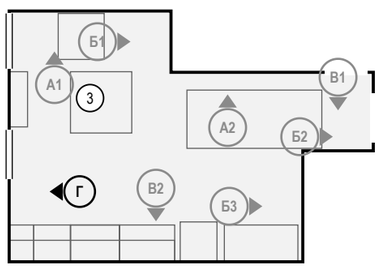

Ведомость отделки (на листе)

Марка	Поверхность	Материал, изделие	Цвет, код	Кол.
О6	плинтус	плинтус МДФ, Orac Decor Contour (Luxxus), h 69 мм, SX165, шелковисто-матовая	NCS S 0300-N	4,1 м
О7	потолок	окраска, Tikkurila, глубокоматовая	NCS S 0300-N	18,9 м²
О8	стены	окраска, Tikkurila, шелковисто-матовая, подготовка Q3	NCS S 1002-Y50R	8,2 м²

Примечания

1. Размеры — в мм от чистовых поверхностей стен; условные обозначения и общие указания — лист 2.
2. Выводы кухонной техники — по утверждённому проекту кухни: привязки выводов даются от осей модулей гарнитура.

					Проект: Квартира 65 м²
	Лист	№ док.	Подпись	Дата	Развёртка стены Г. Кухня-гостиная (пом. 3), кухонный фронт
Дизайнер	Кырлан А.С.			21.10.26	

Стадия	Лист	Листов
П	43	80

выпуск 09.10.2026 № da691793fd · стр. 43 из 80

Правка к этому листу

Развёртка стены А1


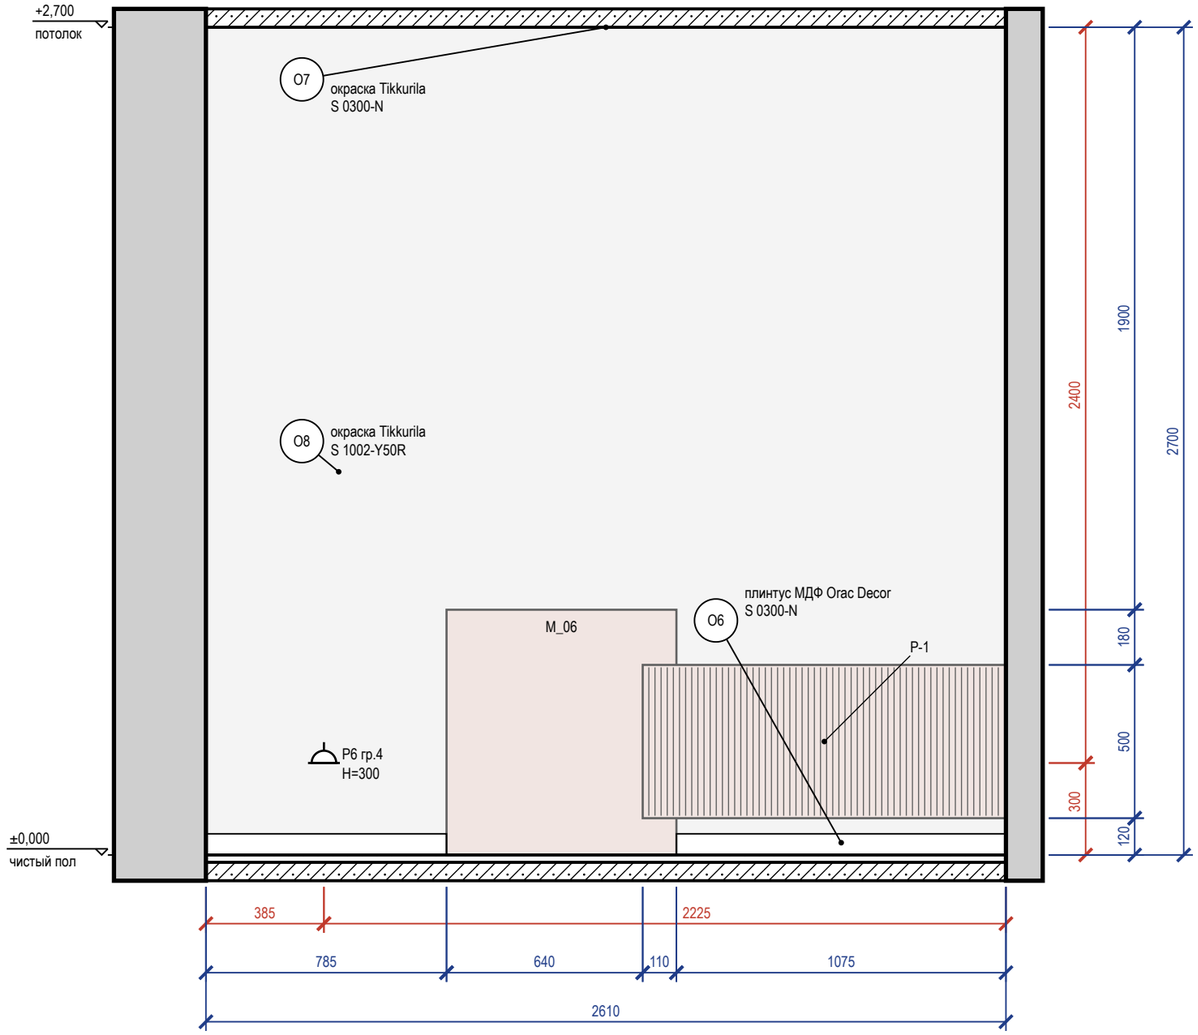


Схема развёрток (М 1:100)

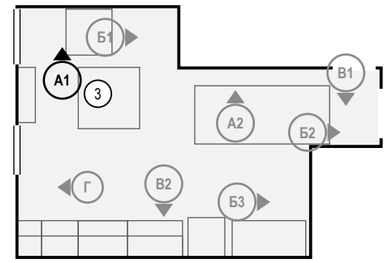

Ведомость отделки (на листе)

Марка	Поверхность	Материал, изделие	Цвет, код	Кол.
О6	плинтус	плинтус МДФ, Orac Decor Contour (Luxxus), h 69 мм, SX165, шелковисто-матовая	NCS S 0300-N	1,9 м
О7	потолок	окраска, Tikkurila, глубокоматовая	NCS S 0300-N	18,9 м²
О8	стены	окраска, Tikkurila, шелковисто-матовая, подготовка Q3	NCS S 1002-Y50R	7 м²

Примечания


1. Размеры — в мм от чистовых поверхностей стен; условные обозначения и общие указания — лист 2.

					Проект: Квартира 65 м²
	Лист	№ док.	Подпись	Дата	Развёртка стены А1. Кухня-гостиная (пом. 3)
Дизайнер	Кырлан А.С.			21.10.26	

Стадия	Лист	Листов
П	44	80

Правка к этому листу

Развёртка стены А2

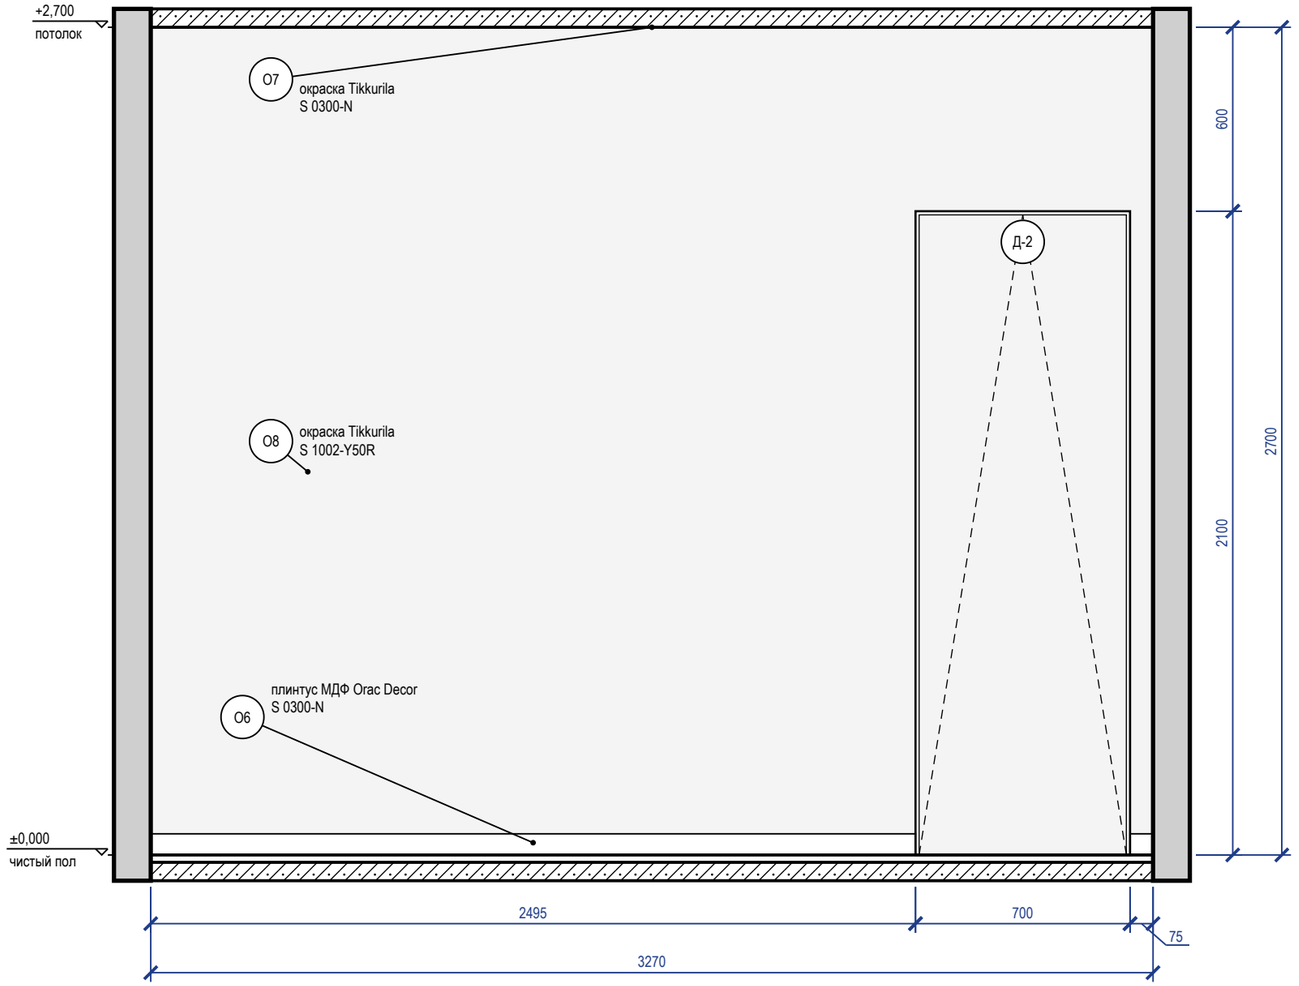

Развёртка стены Б1


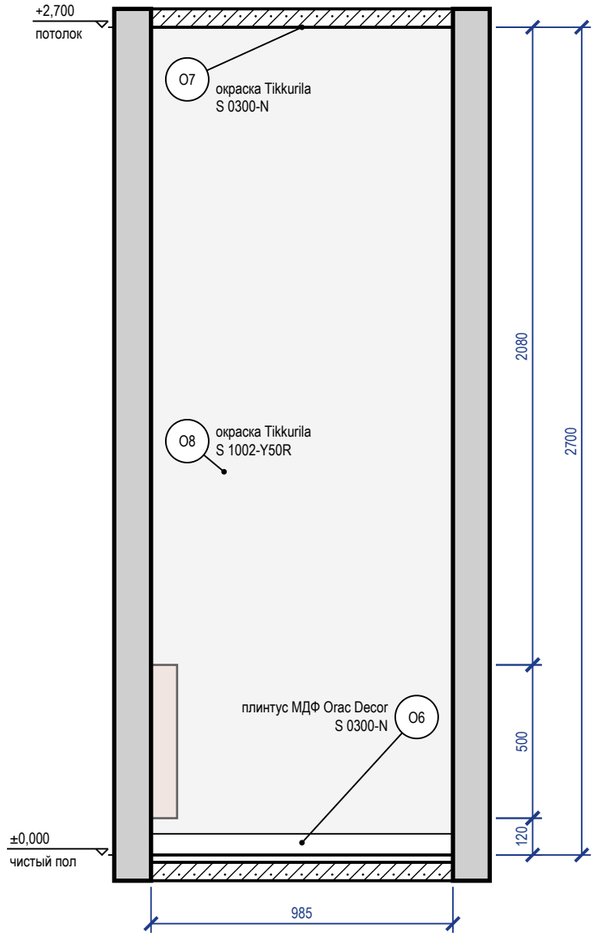


Схема развёрток (М 1:100)

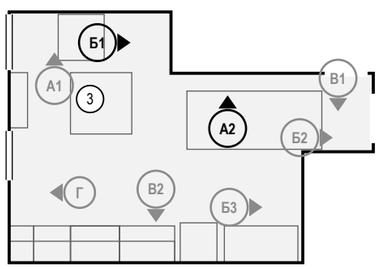

Ведомость отделки (на листе)

Марка	Поверхность	Материал, изделие	Цвет, код	Кол.
О6	плинтус	плинтус МДФ, Orac Decor Contour (Luxxus), h 69 мм, SX165, шелковисто-матовая	NCS S 0300-N	3,6 м
О7	потолок	окраска, Tikkurila, глубокоматовая	NCS S 0300-N	18,9 м²
О8	стены	окраска, Tikkurila, шелковисто-матовая, подготовка Q3	NCS S 1002-Y50R	10 м²

Визуализация этой стены — лист 40



Примечания

1. Размеры — в мм от чистовых поверхностей стен; условные обозначения и общие указания — лист 2.
2. Двери скрытого монтажа — полотно в плоскости стены, отделка стены по полотну, плинтус прерывается у короба (узел — на листе узлов).


					Проект: Квартира 65 м²
	Лист	№ док.	Подпись	Дата	Развёртки стен А2, Б1. Кухня-гостиная (пом. 3)
Дизайнер	Кырлан А.С.			21.10.26	

Стадия	Лист	Листов
П	45	80


выпуск 09.10.2026 № da691793fd · стр. 45 из 80

Правка к этому листу

Развёртка стены Б2

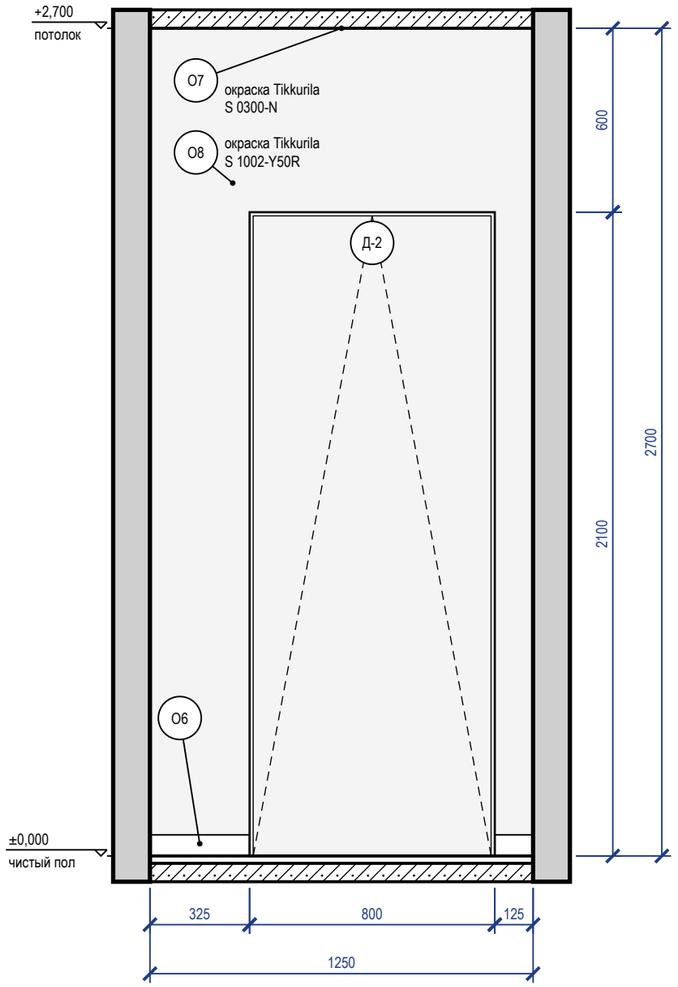

Развёртка стены Б3

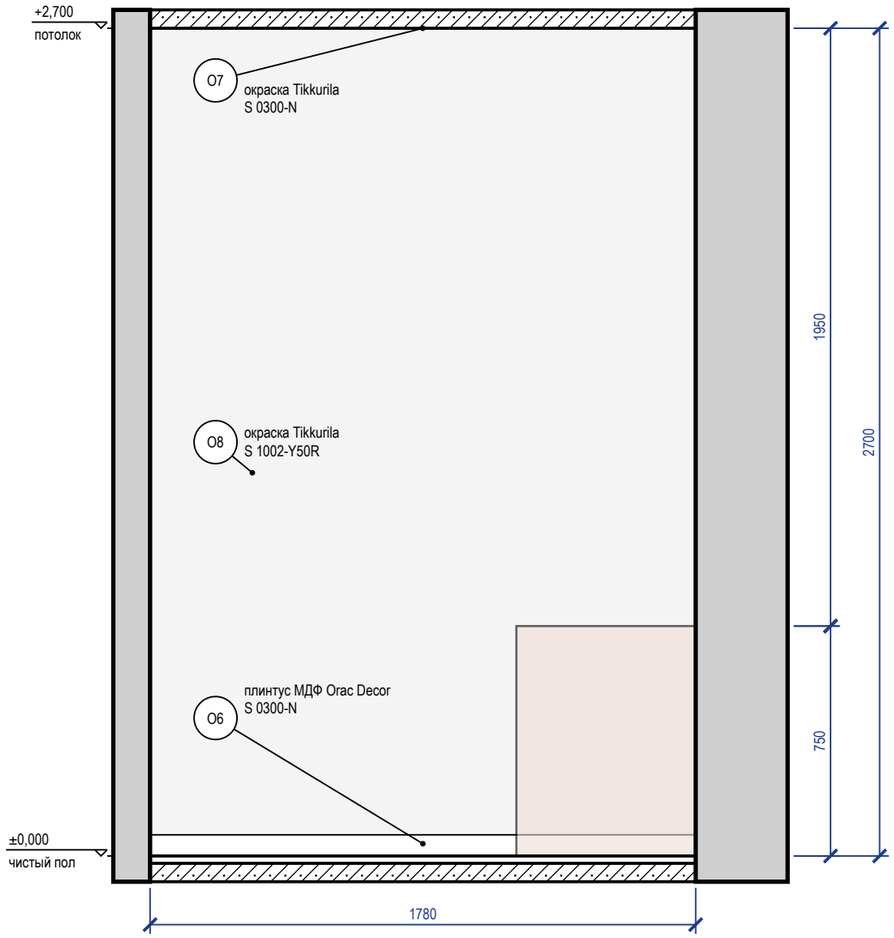

Развёртка стены В1


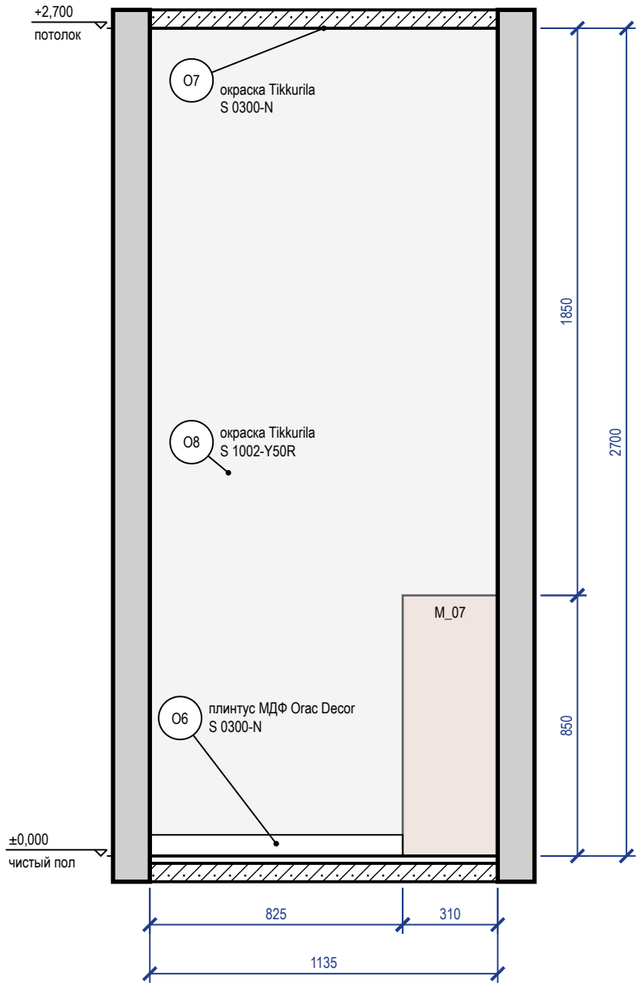


Схема развёрток (М 1:100)

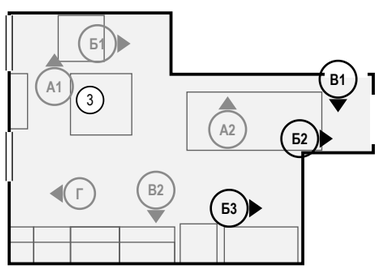

Ведомость отделки (на листе)

Марка	Поверхность	Материал, изделие	Цвет, код	Кол.
О6	плинтус	плинтус МДФ, Orac Decor Contour (Luxxus), h 69 мм, SX165, шелковисто-матовая	NCS S 0300-N	3,1 м
О7	потолок	окраска, Tikkurila, глубокоматовая	NCS S 0300-N	18,9 м²
О8	стены	окраска, Tikkurila, шелковисто-матовая, подготовка Q3	NCS S 1002-Y50R	9,6 м²

Визуализация этой стены — лист 41



Примечания

1. Размеры — в мм от чистовых поверхностей стен; условные обозначения и общие указания — лист 2.
2. Двери скрытого монтажа — полотно в плоскости стены, отделка стены по полотну, плинтус прерывается у короба (узел — на листе узлов).

					Проект: Квартира 65 м²
	Лист	№ док.	Подпись	Дата	Развёртки стен Б2, Б3, В1. Кухня-гостиная (пом. 3)
Дизайнер	Кырлан А.С.			21.10.26	

Стадия	Лист	Листов
П	46	80

выпуск 09.10.2026 № da691793fd · стр. 46 из 80

Правка к этому листу



					Проект: Квартира 65 м²
	Лист	№ док.	Подпись	Дата	
Дизайнер	Кырлан А.С.			21.10.26	Визуализация прихожей

Стадия	Лист	Листов
П	47	80

выпуск 09.10.2026 · da691793fd · стр. 47 из 80

Правка к этому листу




					Проект: Квартира 65 м²
	Лист	№ док.	Подпись	Дата	
Дизайнер	Кырлан А.С.			21.10.26	Визуализация прихожей

Стадия	Лист	Листов
П	48	80

выпуск 09.10.2026 № da691793fd · стр. 48 из 80

Правка к этому листу

Развёртка стены Б

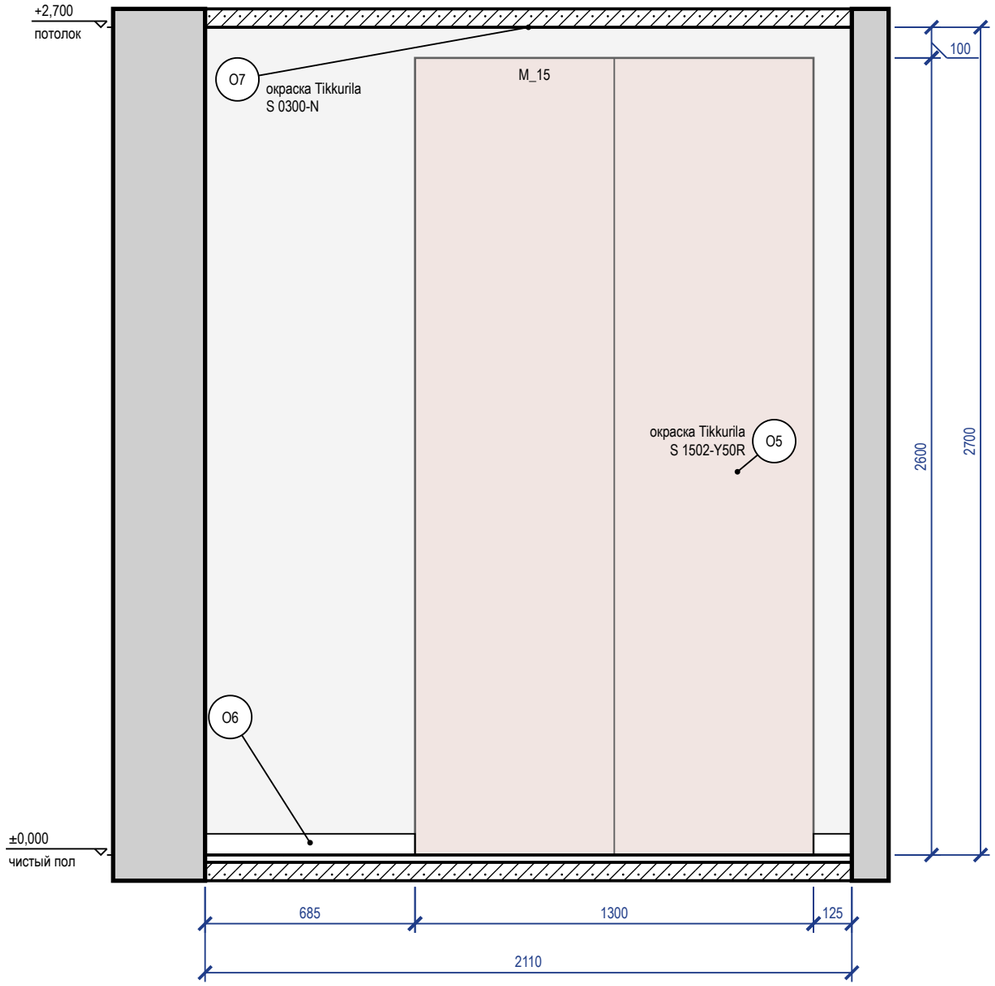

Развёртка стены Г


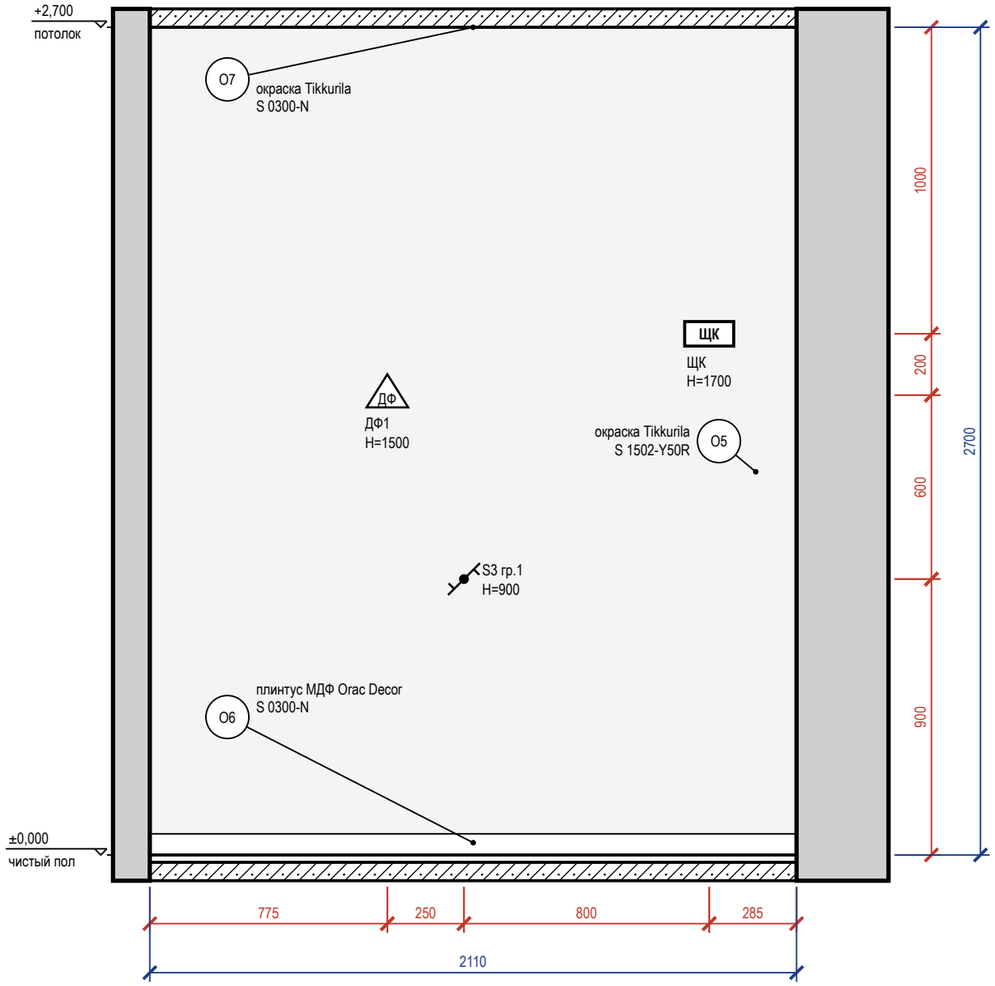


Схема развёрток (М 1:100)

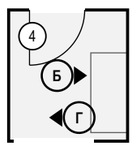

Ведомость отделки (на листе)

Марка	Поверхность	Материал, изделие	Цвет, код	Кол.
О5	стены	окраска, Tikkurila, шелковисто-матовая, подготовка Q3	NCS S 1502-Y50R	11,4 м²
О6	плинтус	плинтус МДФ, Orac Decor Contour (Luxxus), h 69 мм, SX165, шелковисто-матовая	NCS S 0300-N	2,9 м
О7	потолок	окраска, Tikkurila, глубокоматовая	NCS S 0300-N	4,2 м²

Визуализация этой стены — лист 48



Примечания

1. Размеры — в мм от чистовых поверхностей стен; условные обозначения и общие указания — лист 2.

					Проект: Квартира 65 м²
	Лист	№ док.	Подпись	Дата	Развёртки стен. Прихожая (пом. 4)
Дизайнер	Кырлан А.С.			21.10.26	

Стадия	Лист	Листов
П	49	80

выпуск 09.10.2026 № da691793fd · стр. 49 из 80

Правка к этому листу



					Проект: Квартира 65 м²
	Лист	№ док.	Подпись	Дата	
Дизайнер	Кырлан А.С.			21.10.26	Визуализация коридора

Стадия	Лист	Листов
П	50	80

выпуск 09.10.2026 № da691793fd · стр. 50 из 80

Правка к этому листу



					Проект: Квартира 65 м²	
	Лист	№ док.	Подпись	Дата	Визуализация коридора	Стадия / Лист / Листов
Дизайнер	Кырлан А.С.			21.10.26		П / 51 / 80

выпуск 09.10.2026 № da691793fd · стр. 51 из 80

Правка к этому листу

Развёртка стены А


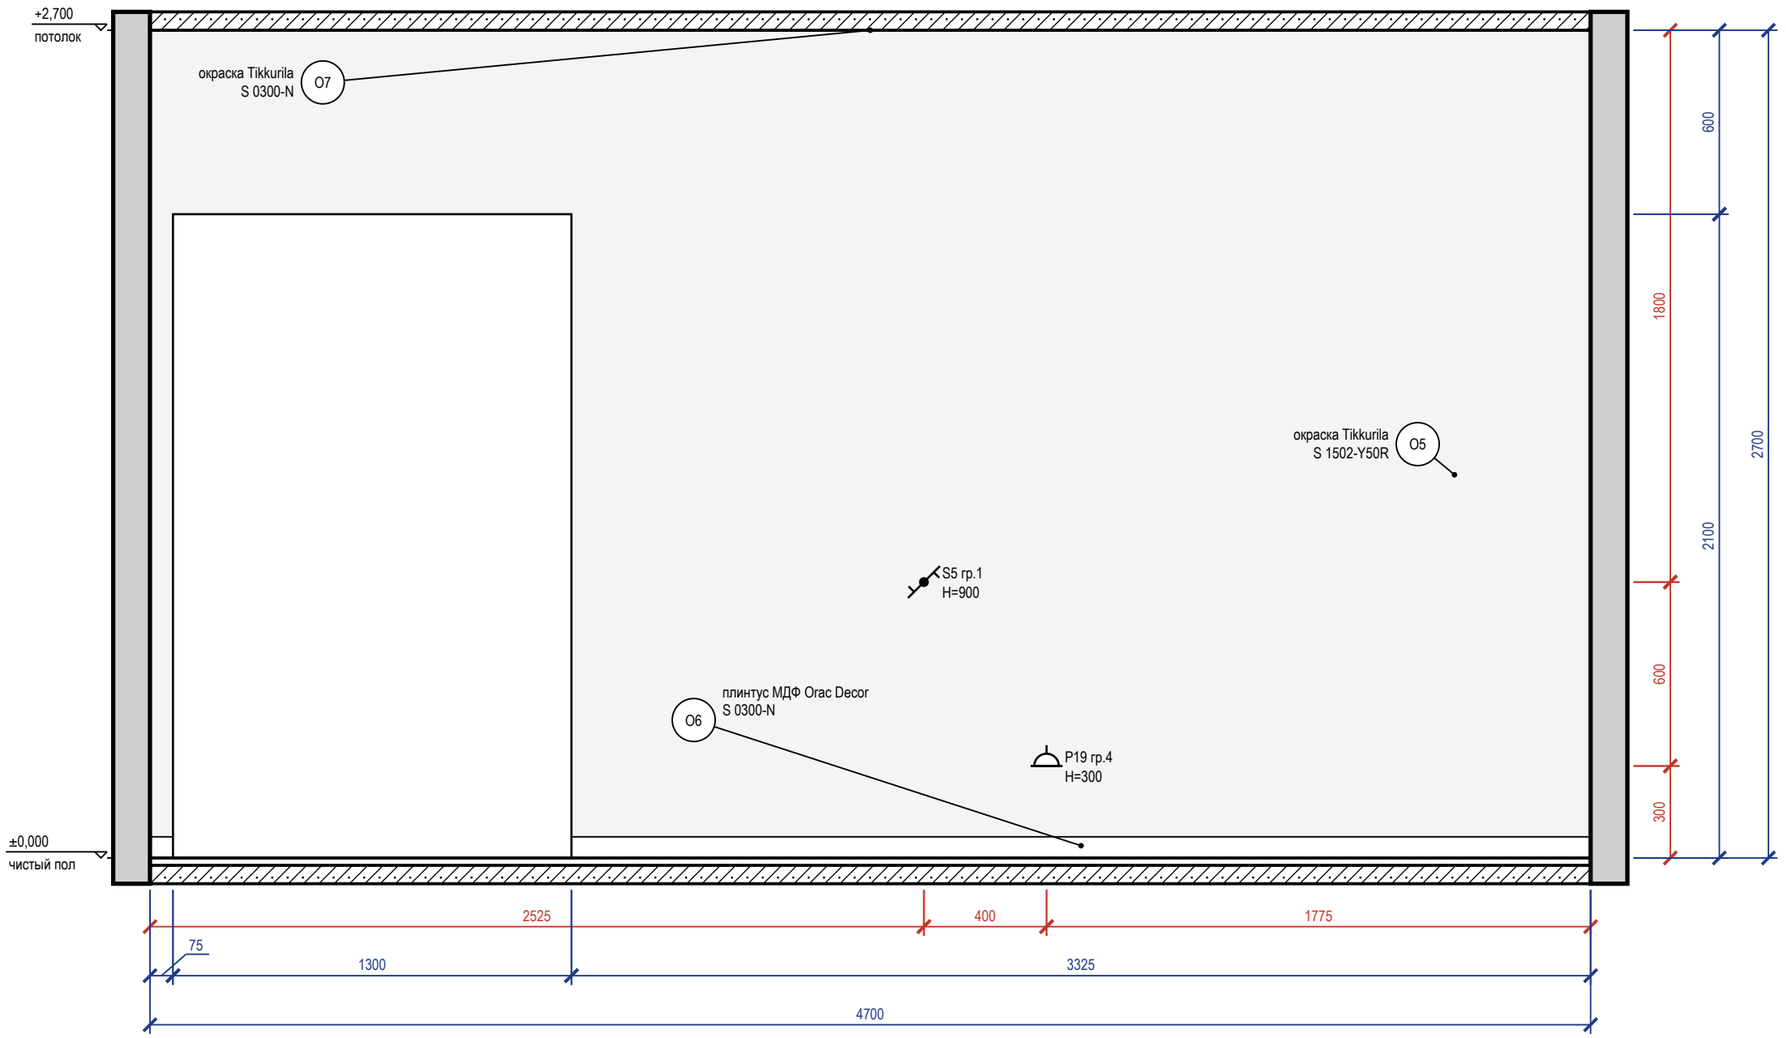


Схема развёрток (М 1:100)

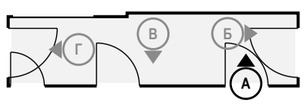

Ведомость отделки (на листе)

Марка	Поверхность	Материал, изделие	Цвет, код	Кол.
О5	стены	окраска, Tikkurila, шелковисто-матовая, подготовка Q3	NCS S 1502-Y50R	10 м²
О6	плинтус	плинтус МДФ, Orac Decor Contour (Luxxus), h 69 мм, SX165, шелковисто-матовая	NCS S 0300-N	3,4 м
О7	потолок	окраска, Tikkurila, глубокоматовая	NCS S 0300-N	5,5 м²

Визуализация этой стены — лист 50



Примечания

1. Размеры — в мм от чистовых поверхностей стен; условные обозначения и общие указания — лист 2.


					Проект: Квартира 65 м²
	Лист	№ док.	Подпись	Дата	Развёртка стены А. Коридор (пом. 5)
Дизайнер	Кырлан А.С.			21.10.26	

Стадия	Лист	Листов
П	52	80

выпуск 09.10.2026 № da691793fd · стр. 52 из 80

Правка к этому листу

Развёртка стены Б

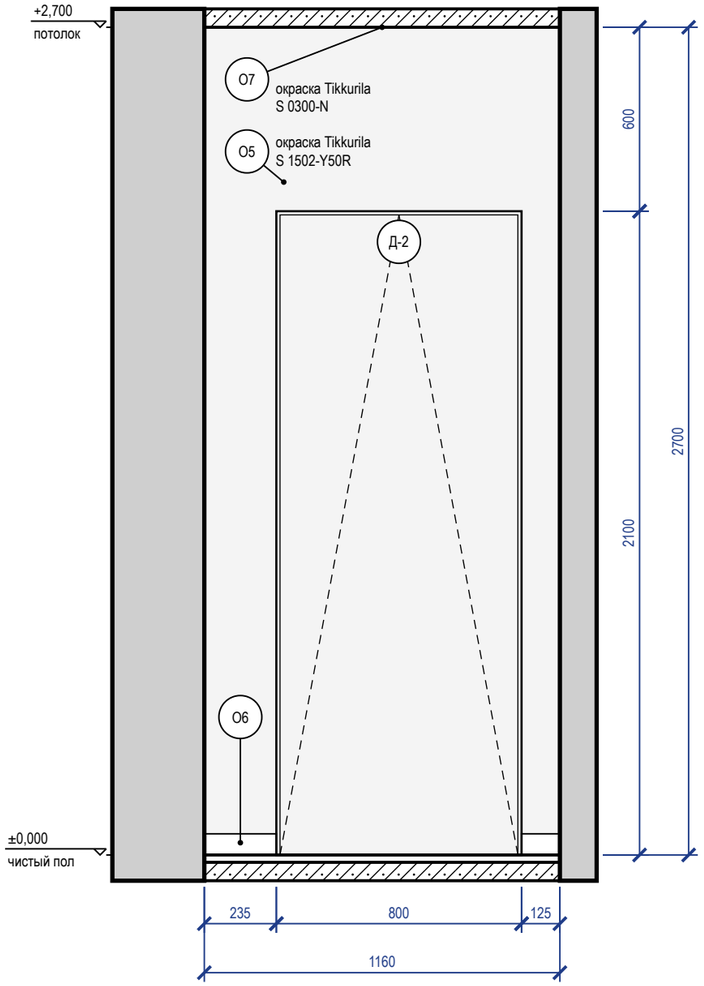

Развёртка стены Г


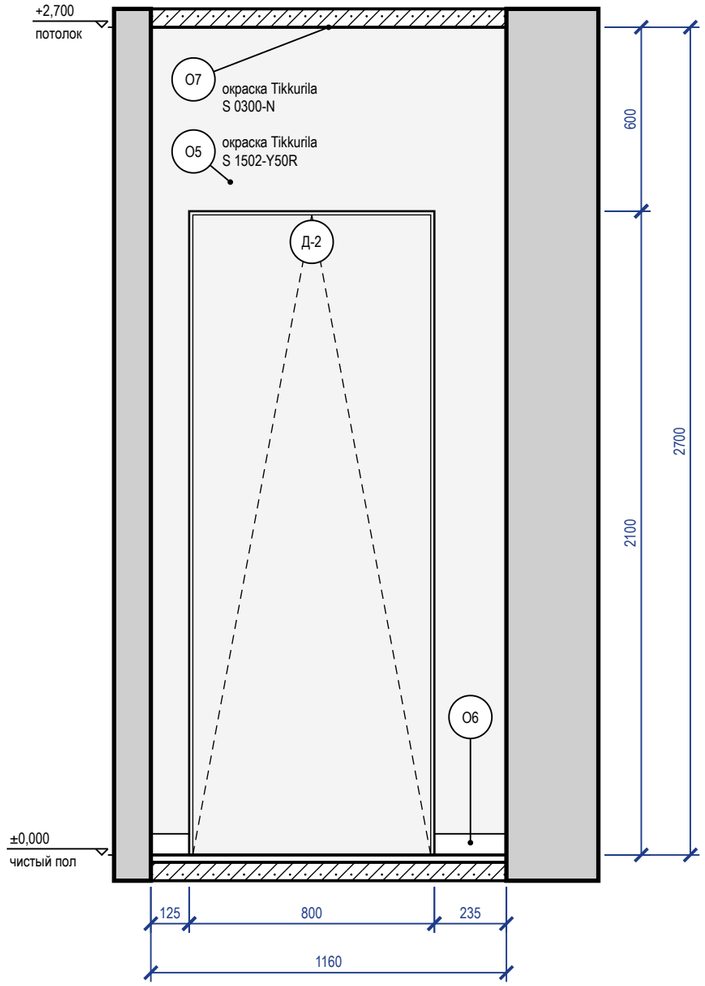


Схема развёрток (М 1:100)

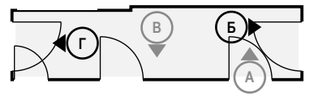

Ведомость отделки (на листе)

Марка	Поверхность	Материал, изделие	Цвет, код	Кол.
О5	стены	окраска, Tikkurila, шелковисто-матовая, подготовка Q3	NCS S 1502-Y50R	2,9 м²
О6	плинтус	плинтус МДФ, Orac Decor Contour (Luxxus), h 69 мм, SX165, шелковисто-матовая	NCS S 0300-N	0,7 м
О7	потолок	окраска, Tikkurila, глубокоматовая	NCS S 0300-N	5,5 м²

Примечания

1. Размеры — в мм от чистовых поверхностей стен; условные обозначения и общие указания — лист 2.
2. Двери скрытого монтажа — полотно в плоскости стены, отделка стены по полотну, плинтус прерывается у короба (узел — на листе узлов).

	Лист	№ док.	Подпись	Дата
Дизайнер	Кырлан А.С.			21.10.26

Проект: Квартира 65 м²


Развёртки стен Б, Г. Коридор (пом. 5)

Стадия	Лист	Листов
П	53	80

выпуск 09.10.2026 № da691793fd · стр. 53 из 80

Правка к этому листу


Развёртка стены В

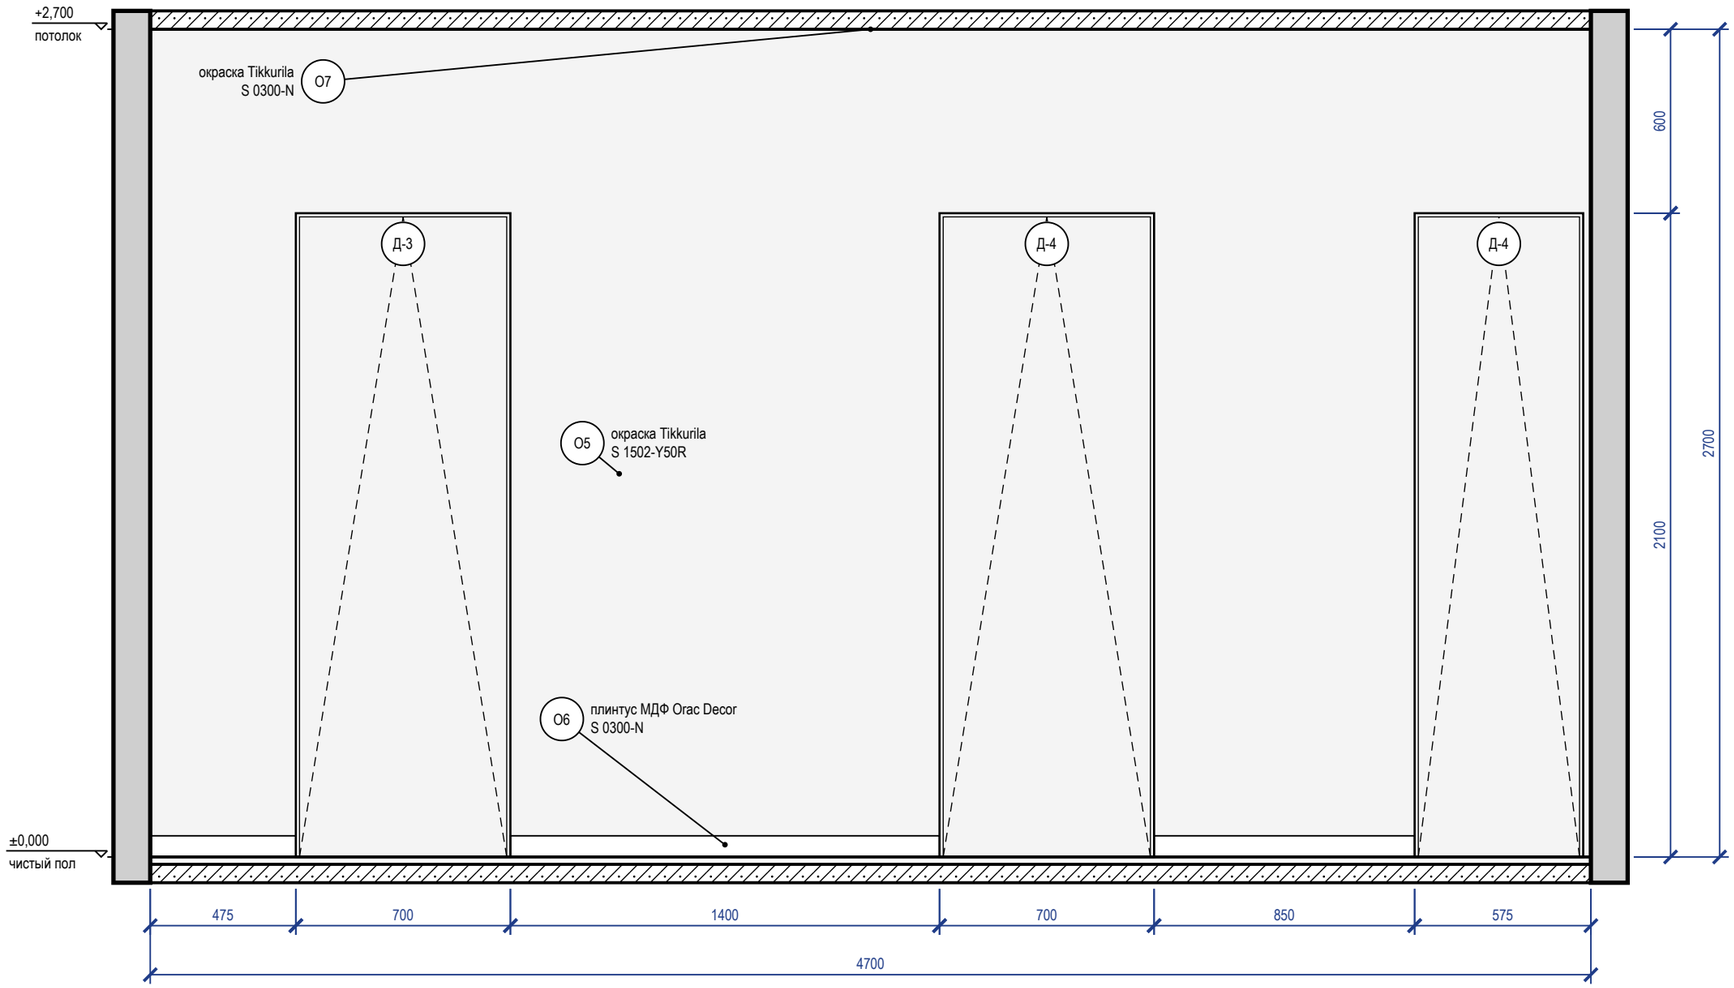

Визуализация этой стены — лист 51



Схема развёрток (М 1:100)

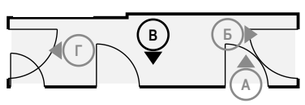

Ведомость отделки (на листе)

Марка	Поверхность	Материал, изделие	Цвет, код	Кол.
О5	стены	окраска, Tikkurila, шелковисто-матовая, подготовка Q3	NCS S 1502-Y50R	8,6 м²
О6	плинтус	плинтус МДФ, Orac Decor Contour (Luxxus), h 69 мм, SX165, шелковисто-матовая	NCS S 0300-N	2,7 м
О7	потолок	окраска, Tikkurila, глубокоматовая	NCS S 0300-N	5,5 м²

Примечания

1. Размеры — в мм от чистовых поверхностей стен; условные обозначения и общие указания — лист 2.
2. Двери скрытого монтажа — полотно в плоскости стены, отделка стены по полотну, плинтус прерывается у короба (узел — на листе узлов).

					Проект: Квартира 65 м²
	Лист	№ док.	Подпись	Дата	Развёртка стены В. Коридор (пом. 5)
Дизайнер	Кырлан А.С.			21.10.26	

Стадия	Лист	Листов
П	54	80

выпуск 09.10.2026 № da691793fd · стр. 54 из 80

Правка к этому листу




					Проект: Квартира 65 м²	
	Лист	№ док.	Подпись	Дата	Визуализация санузла	Стадия / Лист / Листов
Дизайнер	Кырлан А.С.			21.10.26		П / 55 / 80


выпуск 09.10.2026 · da691793fd · стр. 55 из 80

Правка к этому листу

Развёртка стены А

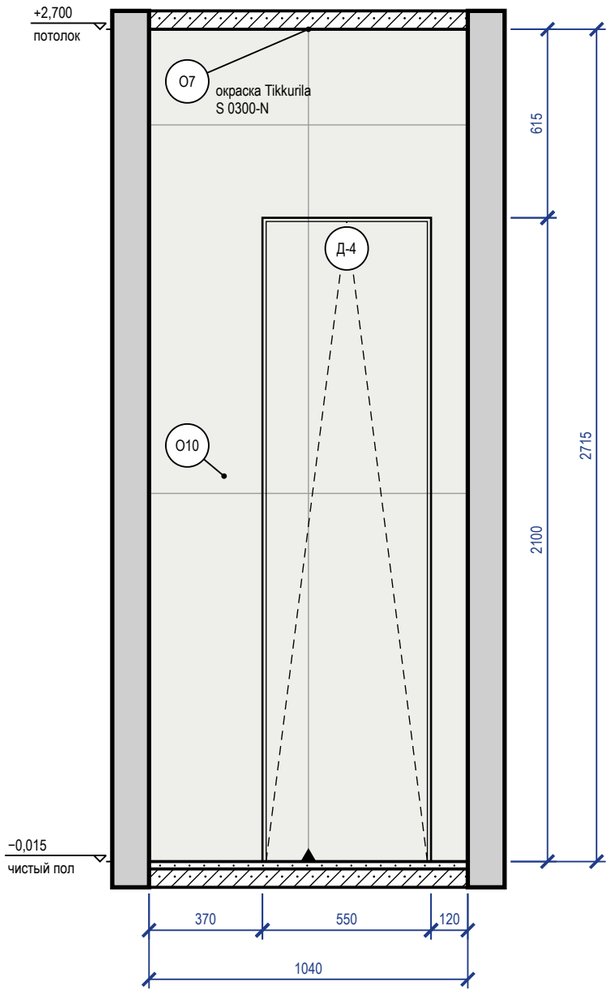

Развёртка стены Б

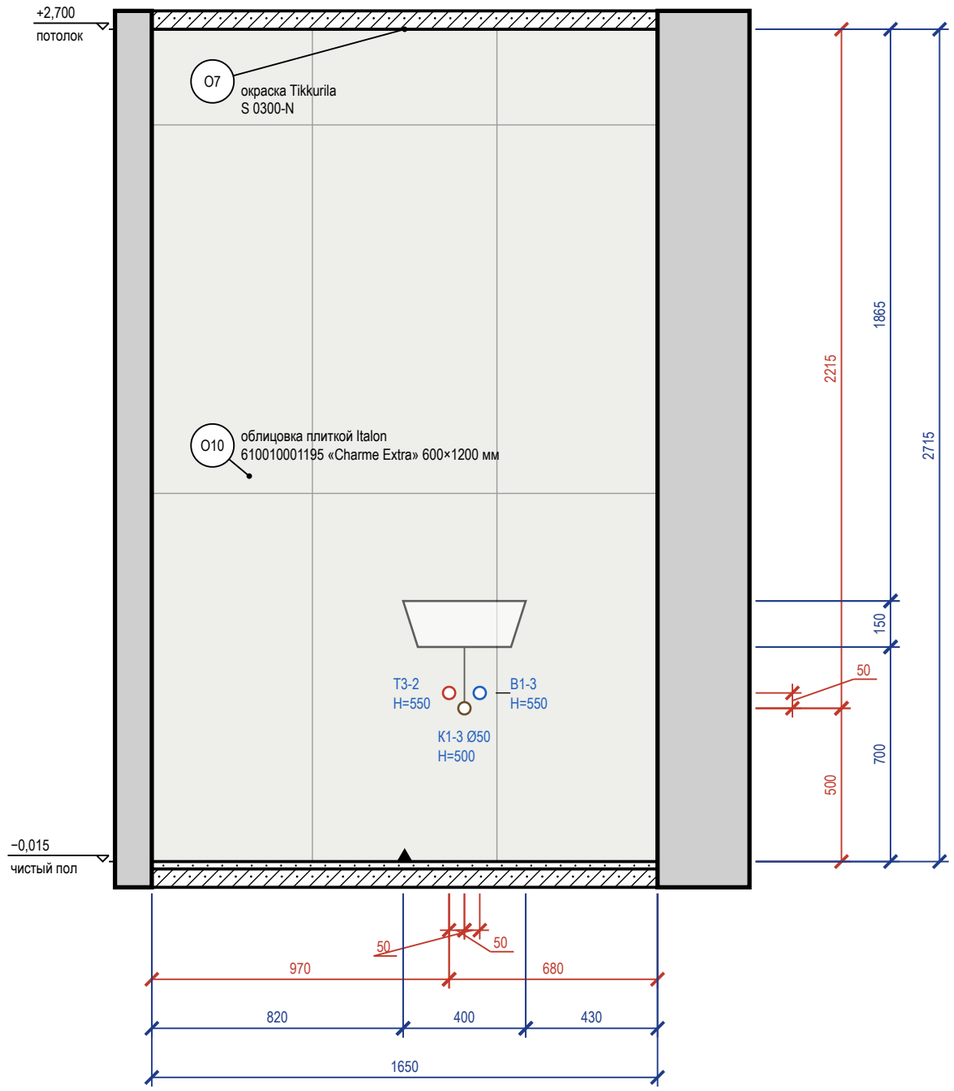

Развёртка стены В


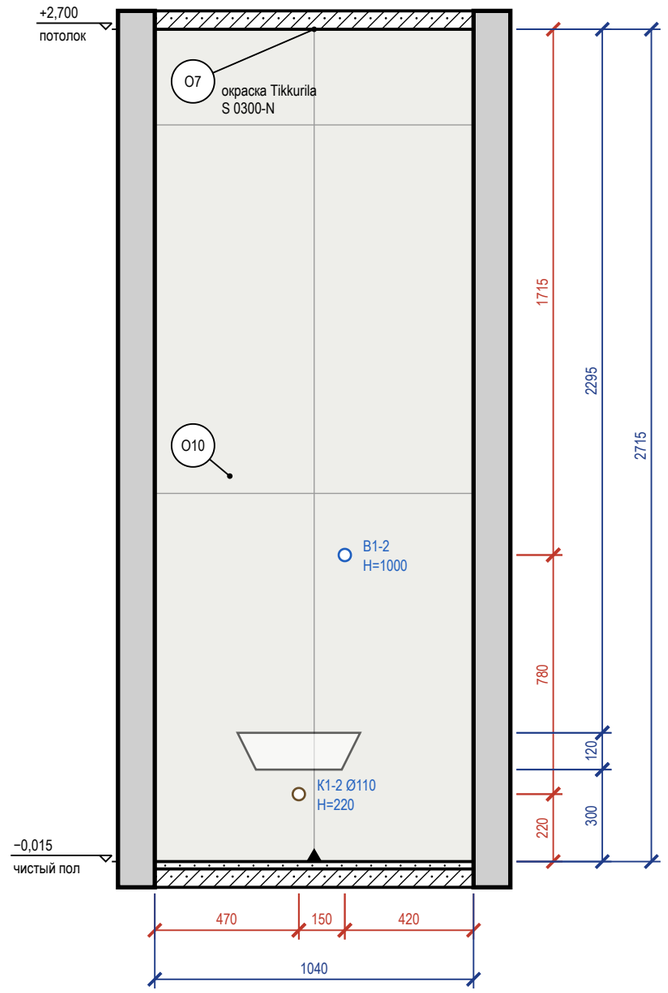


Схема развёрток (М 1:100)

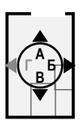

Ведомость отделки (на листе)

Марка	Поверхность	Материал, изделие	Цвет, код	Кол.
О7	потолок	окраска, Tikkurila, глубокоматовая	NCS S 0300-N	1,8 м²
О10	стены	облицовка плиткой, Italon Charme Extra, 600×1200 мм, 610010001195	Italon 610010001195 «Charme Extra»	9 м²

Визуализация этой стены — лист 55



Примечания

1. Размеры — в мм от чистовых поверхностей стен; условные обозначения и общие указания — лист 2.
2. Схема мебели, приборов и декора не является технической документацией для производства мебели; габариты — по паспортам изделий.
3. Облицовка — по сетке швов, раскладка от оси стены (треугольник у пола); подрезки — по листу раскладки плитки.
4. Гидроизоляция в 2 слоя, заход на стены 200 мм — до облицовки, с актом скрытых работ и тестом проливом (узел — на листе узлов).
5. Двери скрытого монтажа — полотно в плоскости стены, отделка стены по полотну, плинтус прерывается у короба (узел — на листе узлов).

					Проект: Квартира 65 м²
	Лист	№ док.	Подпись	Дата	Развёртки стен А, Б, В. Санузел (пом. 6)
Дизайнер	Кырлан А.С.			21.10.26	

Стадия	Лист	Листов
П	56	80

выпуск 09.10.2026 № da691793fd · стр. 56 из 80

Правка к этому листу

Развёртка стены Г


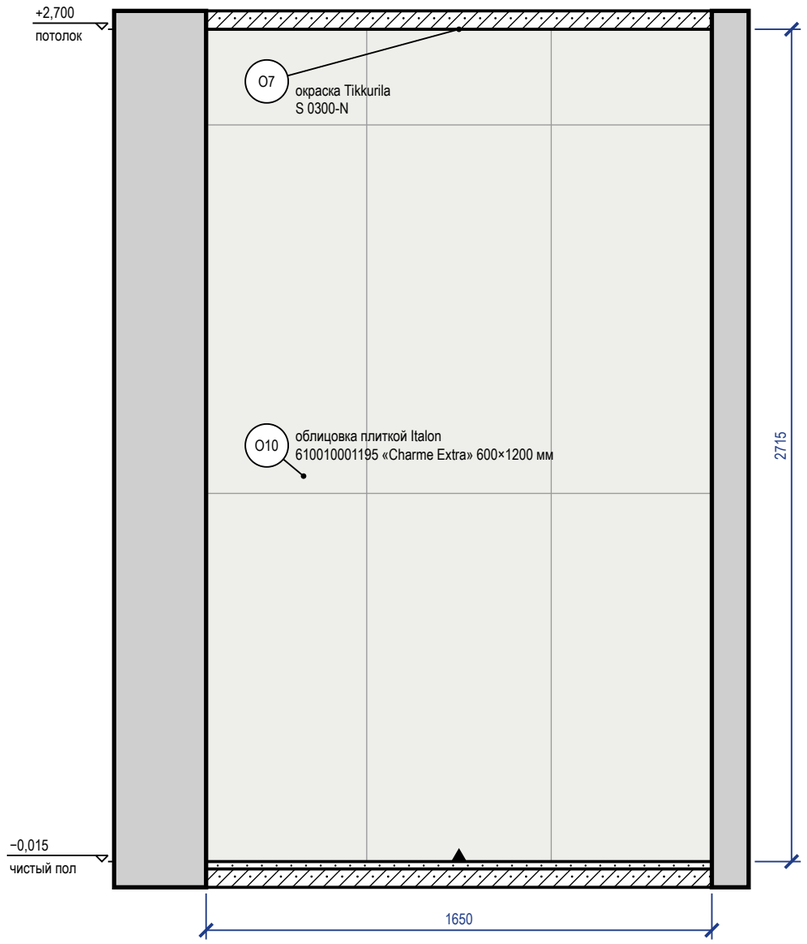


Схема развёрток (М 1:100)

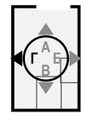


Ведомость отделки (на листе)

Марка	Поверхность	Материал, изделие	Цвет, код	Кол.
О7	потолок	окраска, Tikkurila, глубокоматовая	NCS S 0300-N	1,8 м²
О10	стены	облицовка плиткой, Italon Charme Extra, 600×1200 мм, 610010001195	Italon 610010001195 «Charme Extra»	4,5 м²

3 Короб стояков К1-1 с люком и звукоизоляцией (М 1:20)

Узел 3 — лист С3

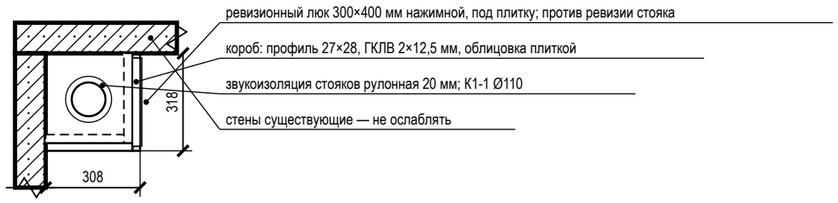

Примечания

1. Размеры — в мм от чистовых поверхностей стен; условные обозначения и общие указания — лист 2.
2. Облицовка — по сетке швов, раскладка от оси стены (треугольник у пола); подрезки — по листу раскладки плитки.
3. Гидроизоляция в 2 слоя, заход на стены 200 мм — до облицовки, с актом скрытых работ и тестом проливом (узел — на листе узлов).

					Проект: Квартира 65 м²
	Лист	№ док.	Подпись	Дата	Развёртка стены Г. Санузел (пом. 6)
Дизайнер	Кырлан А.С.			21.10.26	

Стадия	Лист	Листов
П	57	80

Правка к этому листу



					Проект: Квартира 65 м²	
	Лист	№ док.	Подпись	Дата	Визуализация ванной	Стадия / Лист / Листов
Дизайнер	Кырлан А.	С.		21.10.26		П / 58 / 80

выпуск 09.10.2026 № da691793fd · стр. 58 из 80

Правка к этому листу




					Проект: Квартира 65 м²
	Лист	№ док.	Подпись	Дата	
Дизайнер	Кырлан А.С.			21.10.26	Визуализация ванной

Стадия	Лист	Листов
П	59	80

выпуск 09.10.2026 da691793fd · стр. 59 из 80

Правка к этому листу

Развёртка стены А

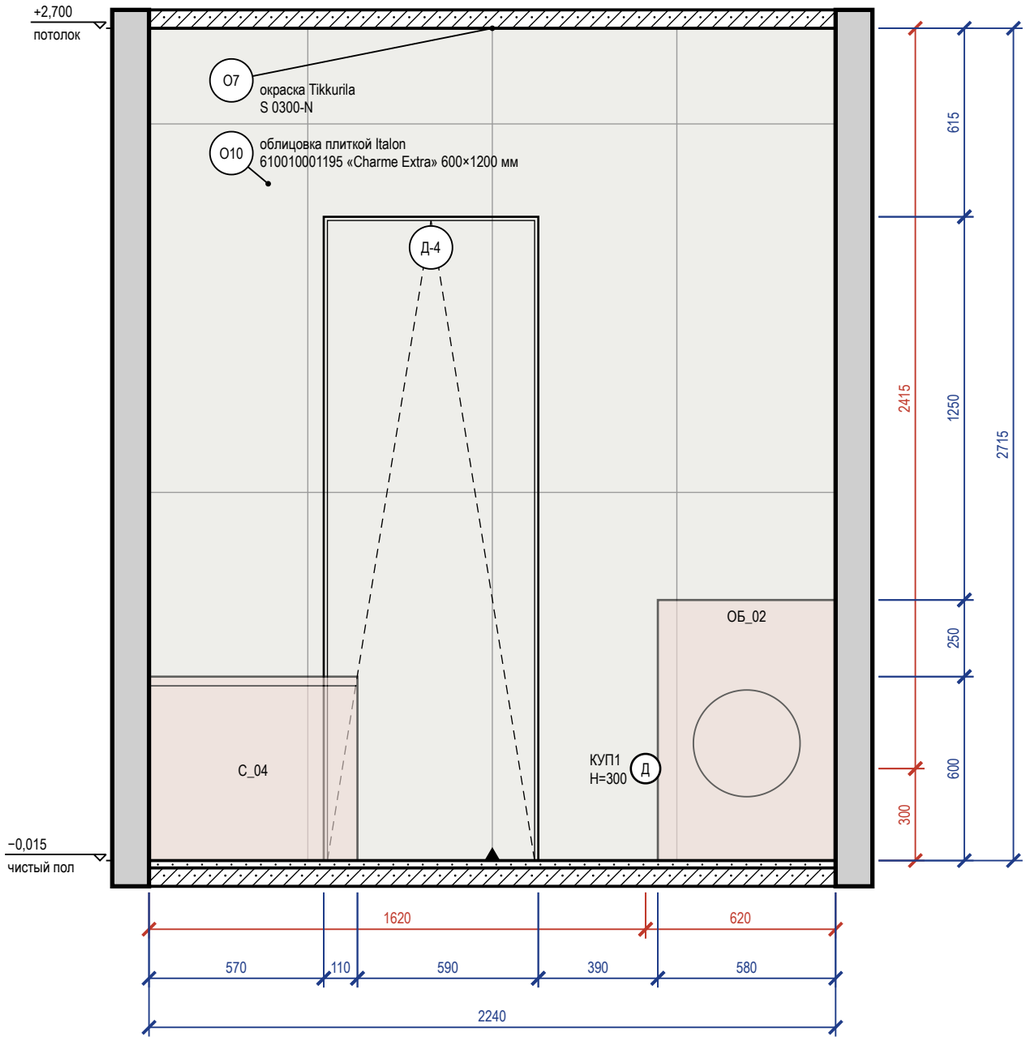

Развёртка стены Б


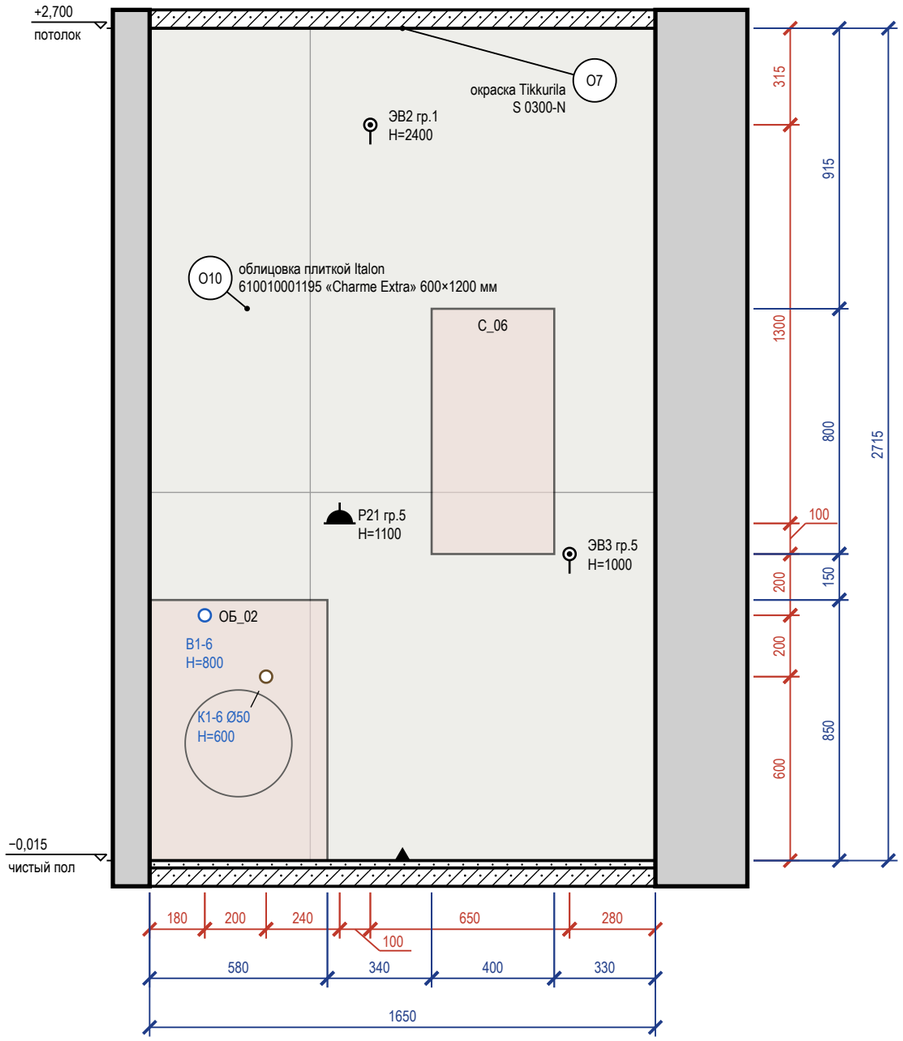



Схема развёрток (М 1:100)

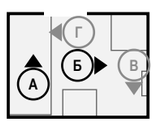

Ведомость отделки (на листе)

Марка	Поверхность	Материал, изделие	Цвет, код	Кол.
О7	потолок	окраска, Tikkurila, глубокоматовая	NCS S 0300-N	3,9 м²
О10	стены	облицовка плиткой, Italon Charme Extra, 600×1200 мм, 610010001195	Italon 610010001195 «Charme Extra»	9,1 м²

Визуализация этой стены — лист 59

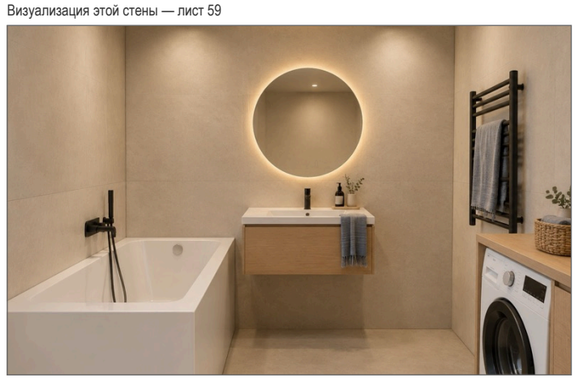

Примечания

1. Размеры — в мм от чистовых поверхностей стен; условные обозначения и общие указания — лист 2.
2. Схема мебели, приборов и декора не является технической документацией для производства мебели; габариты — по паспортам изделий.
3. Облицовка — по сетке швов, раскладка от оси стены (треугольник у пола); подрезки — по листу раскладки плитки.
4. Гидроизоляция в 2 слоя, заход на стены 200 мм — до облицовки, с актом скрытых работ и тестом проливом (узел — на листе узлов).
5. Двери скрытого монтажа — полотно в плоскости стены, отделка стены по полотну, плинтус прерывается у короба (узел — на листе узлов).


					Проект: Квартира 65 м²
	Лист	№ док.	Подпись	Дата	Развёртки стен А, Б. Ванная (пом. 7)
Дизайнер	Кырлан А.С.			21.10.26	

Стадия	Лист	Листов
П	60	80

выпуск 09.10.2026 № da691793fd · стр. 60 из 80

Правка к этому листу

Развёртка стены В

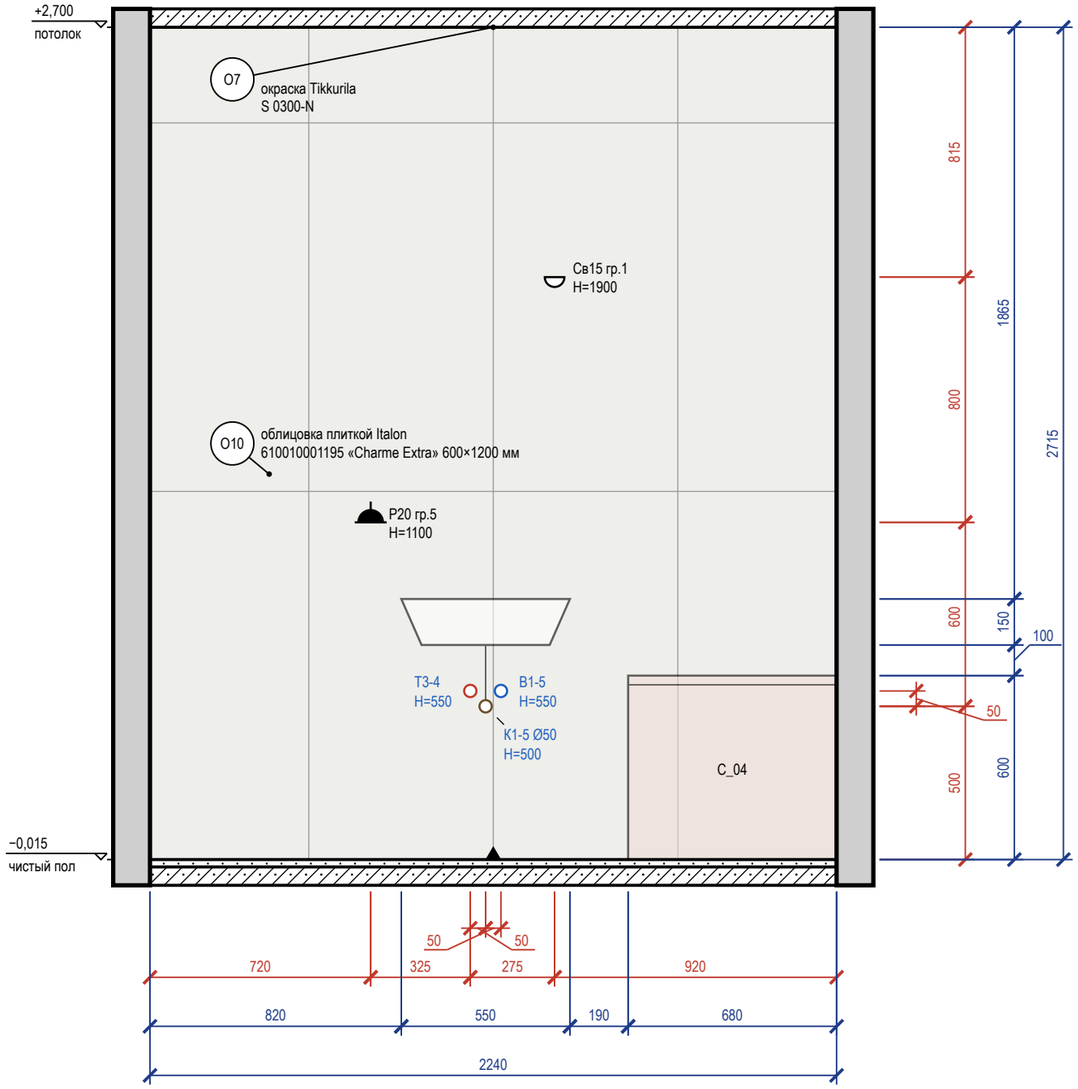

Развёртка стены Г


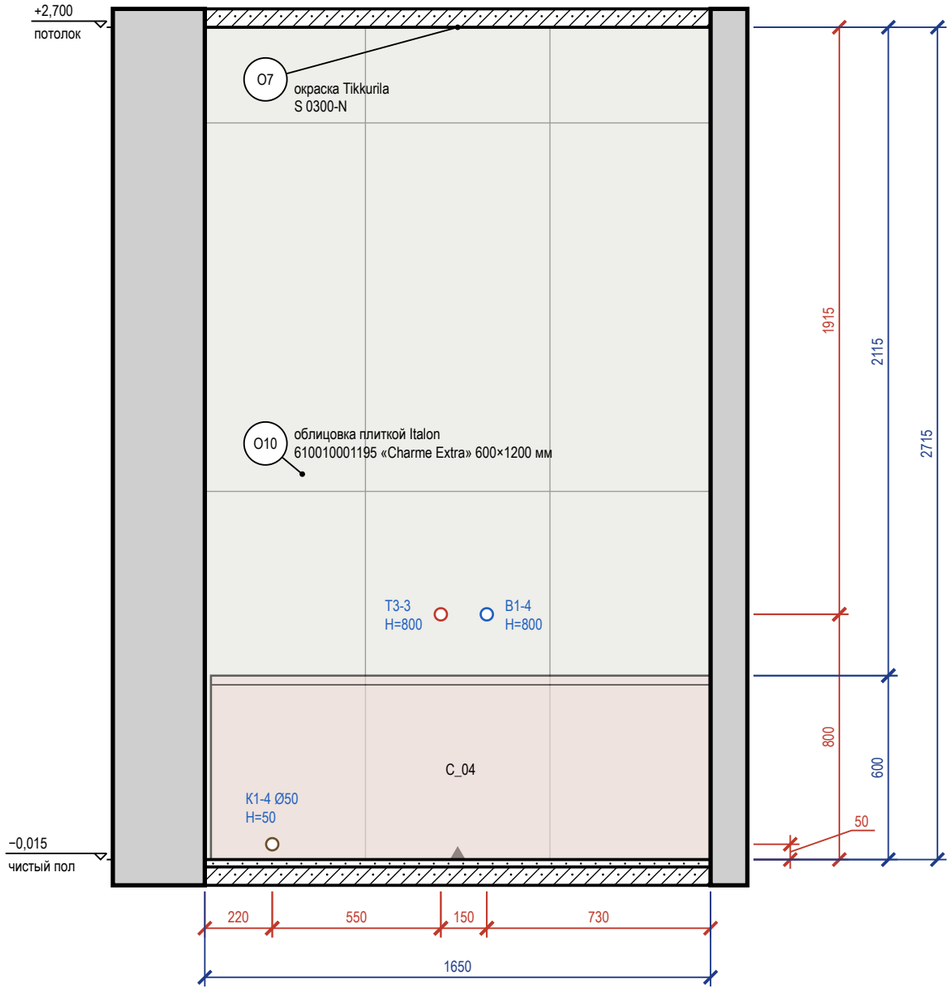


Схема развёрток (М 1:100)

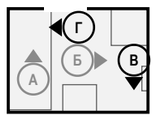

Ведомость отделки (на листе)

Марка	Поверхность	Материал, изделие	Цвет, код	Кол.
О7	потолок	окраска, Tikkurila, глубокоматовая	NCS S 0300-N	3,9 м²
О10	стены	облицовка плиткой, Italon Charme Extra, 600×1200 мм, 610010001195	Italon 610010001195 «Charme Extra»	10,6 м²

Визуализация этой стены — лист 58



Примечания

1. Размеры — в мм от чистовых поверхностей стен; условные обозначения и общие указания — лист 2.
2. Облицовка — по сетке швов, раскладка от оси стены (треугольник у пола); подрезки — по листу раскладки плитки.
3. Гидроизоляция в 2 слоя, заход на стены 200 мм — до облицовки, с актом скрытых работ и тестом проливом (узел — на листе узлов).

					Проект: Квартира 65 м²
	Лист	№ док.	Подпись	Дата	Развёртки стен В, Г. Ванная (пом. 7)
Дизайнер	Кырлан А.С.			21.10.26	

Стадия	Лист	Листов
П	61	80

выпуск 09.10.2026 № da691793fd · стр. 61 из 80

Правка к этому листу




					Проект: Квартира 65 м²	
	Лист	№ док.	Подпись	Дата	Визуализация кладовой	Стадия / Лист / Листов
Дизайнер	Кырлан А.С.			21.10.26		П / 62 / 80

выпуск 09.10.2026 № da691793fd · стр. 62 из 80

Правка к этому листу

Развёртка стены А

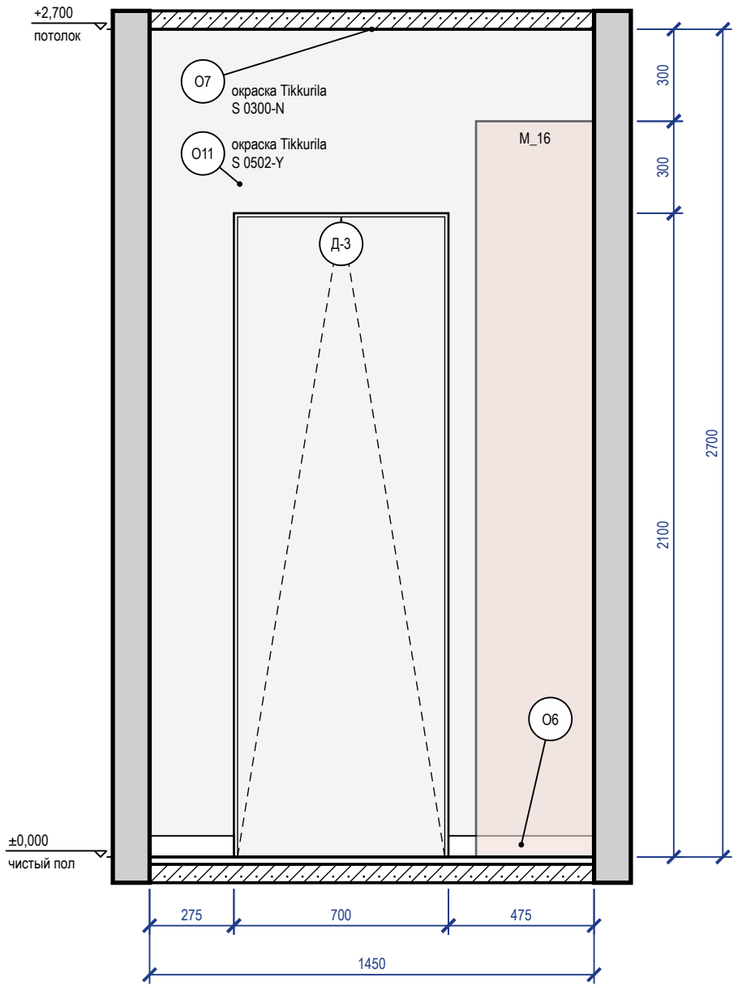

Развёртка стены Б


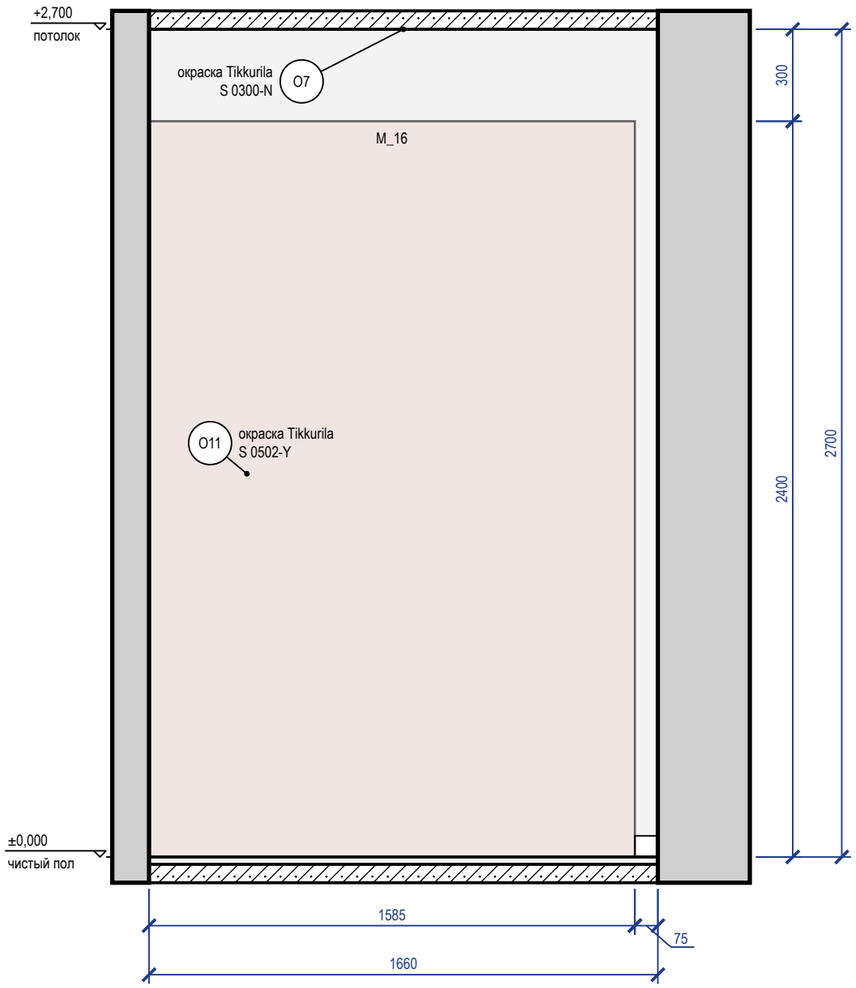


Схема развёрток (М 1:100)

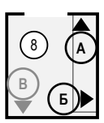

Ведомость отделки (на листе)

Марка	Поверхность	Материал, изделие	Цвет, код	Кол.
О6	плинтус	плинтус МДФ, Orac Decor Contour (Luxxus), h 69 мм, SX165, шелковисто-матовая	NCS S 0300-N	0,8 м
О7	потолок	окраска, Tikkurila, глубокоматовая	NCS S 0300-N	2,5 м²
О11	стены	окраска, Tikkurila, матовая, подготовка Q3	NCS S 0502-Y	6,9 м²

Примечания

1. Размеры — в мм от чистовых поверхностей стен; условные обозначения и общие указания — лист 2.
2. Двери скрытого монтажа — полотно в плоскости стены, отделка стены по полотну, плинтус прерывается у короба (узел — на листе узлов).

					Проект: Квартира 65 м²
	Лист	№ док.	Подпись	Дата	Развёртки стен А, Б. Кладовая (пом. 8)
Дизайнер	Кырлан А.С.			21.10.26	

Стадия	Лист	Листов
П	63	80

выпуск 09.10.2026 № da691793fd · стр. 63 из 80

Правка к этому листу

Развёртка стены В


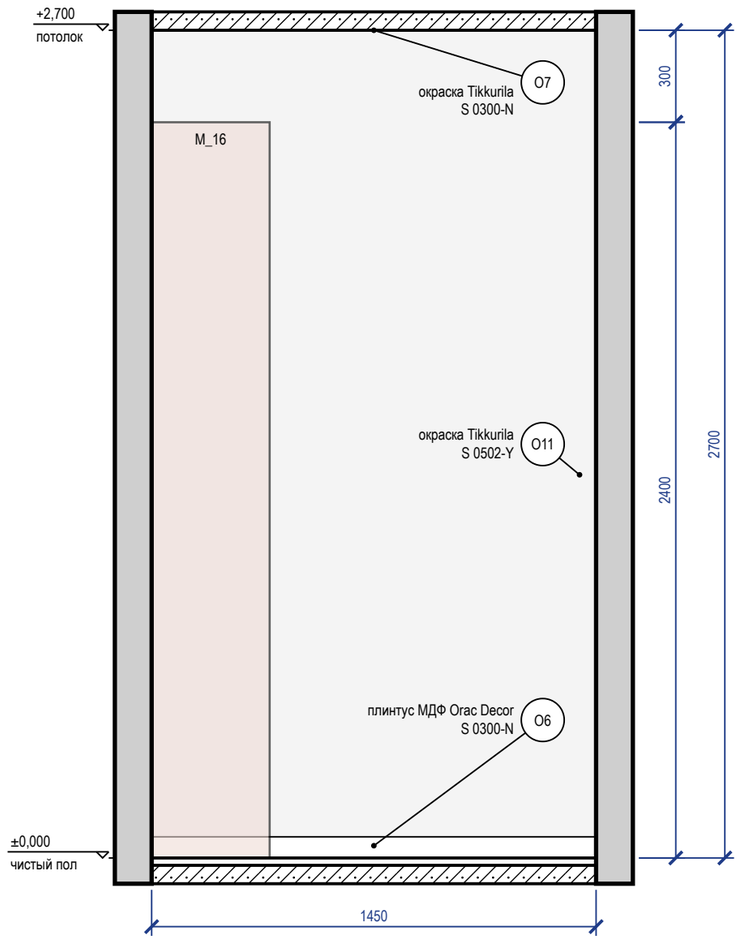


Схема развёрток (М 1:100)

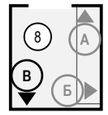

Ведомость отделки (на листе)

Марка	Поверхность	Материал, изделие	Цвет, код	Кол.
O6	плинтус	плинтус МДФ, Orac Decor Contour (Luxxus), h 69 мм, SX165, шелковисто-матовая	NCS S 0300-N	1,4 м
O7	потолок	окраска, Tikkurila, глубокоматовая	NCS S 0300-N	2,5 м²
O11	стены	окраска, Tikkurila, матовая, подготовка Q3	NCS S 0502-Y	3,9 м²

Визуализация этой стены — лист 62



Примечания

1. Размеры — в мм от чистовых поверхностей стен; условные обозначения и общие указания — лист 2.

					Проект: Квартира 65 м²
	Лист	№ док.	Подпись	Дата	
Дизайнер	Кырлан А.С.			21.10.26	Развёртка стены В. Кладовая (пом. 8)

Стадия	Лист	Листов
П	64	80

выпуск 09.10.2026 № da691793fd · стр. 64 из 80

Правка к этому листу



					Проект: Квартира 65 м²
	Лист	№ док.	Подпись	Дата	
Дизайнер	Кырлан А.С.			21.10.26	Визуализация детской

Стадия	Лист	Листов
П	65	80

выпуск 09.10.2026 № da691793fd · стр. 65 из 80

Правка к этому листу



					Проект: Квартира 65 м²	
	Лист	№ док.	Подпись	Дата	Визуализация детской	Стадия / Лист / Листов
Дизайнер	Кырлан А.С.			21.10.26		П / 66 / 80

выпуск 09.10.2026 № da691793fd · стр. 66 из 80

Правка к этому листу



					Проект: Квартира 65 м²
	Лист	№ док.	Подпись	Дата	
Дизайнер	Кырлан А.С.			21.10.26	Визуализация детской

Стадия	Лист	Листов
П	67	80

Правка к этому листу



					Проект: Квартира 65 м²	
	Лист	№ док.	Подпись	Дата		
Дизайнер	Кырлан А.С.			21.10.26	Визуализация детской	Стадия: П; Лист: 68; Листов: 80

выпуск 09.10.2026 № da691793fd · стр. 68 из 80

Правка к этому листу

Развёртка стены А


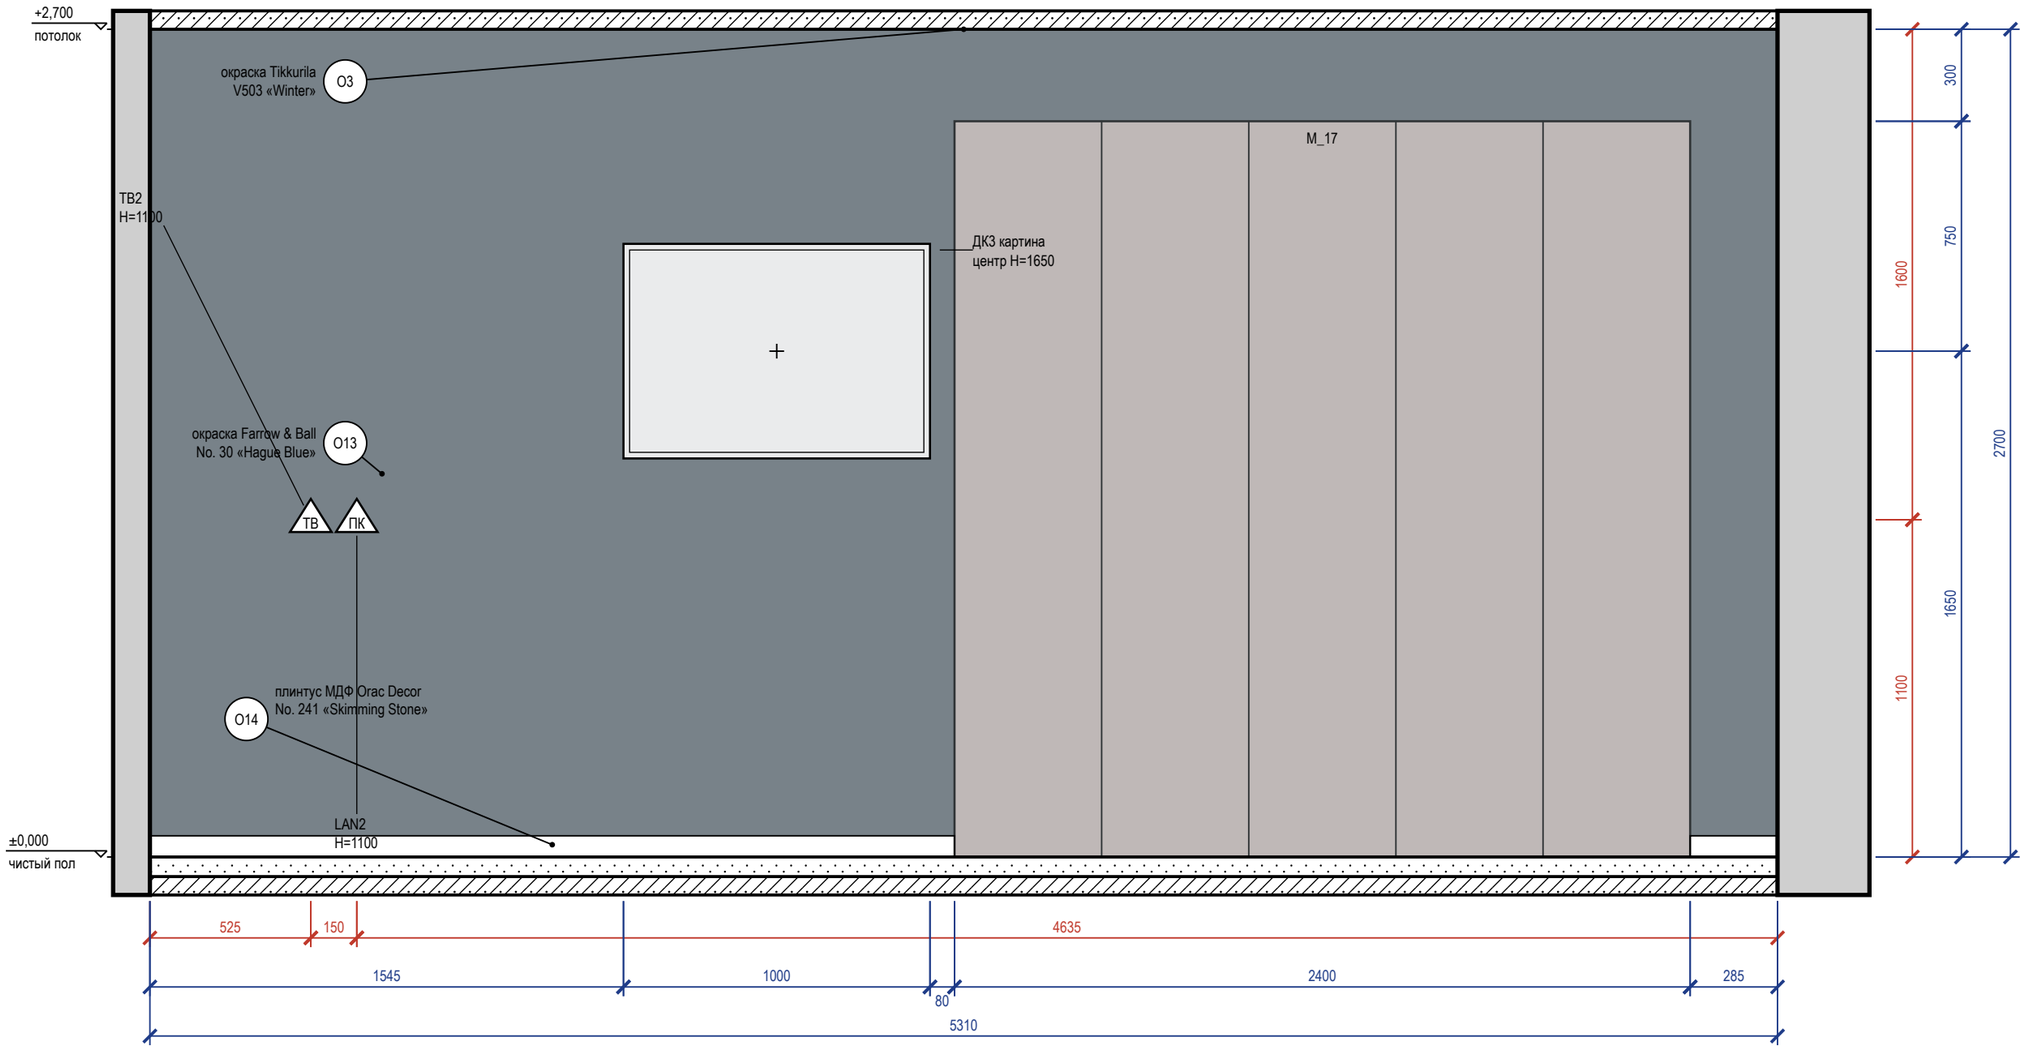



Схема развёрток (М 1:100)

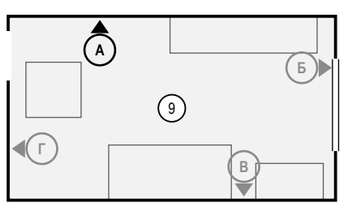

Ведомость отделки (на листе)

Марка	Поверхность	Материал, изделие	Цвет, код	Кол.
О3	потолок	окраска, Tikkurila Anti-Reflex 2, глубокоматовая, подготовка Q3	Tikkurila V503 «Winter»	16 м²
О13	акцентная стена	окраска, Farrow & Ball Modern Emulsion, матовая, подготовка Q3	Farrow & Ball No. 30 «Hague Blue»	14,3 м²
О14	плинтус	плинтус МДФ, Orac Decor Contour (Luxxus), h 69 мм, SX165	Farrow & Ball No. 241 «Skimming Stone»	2,9 м

Визуализация этой стены — лист 66

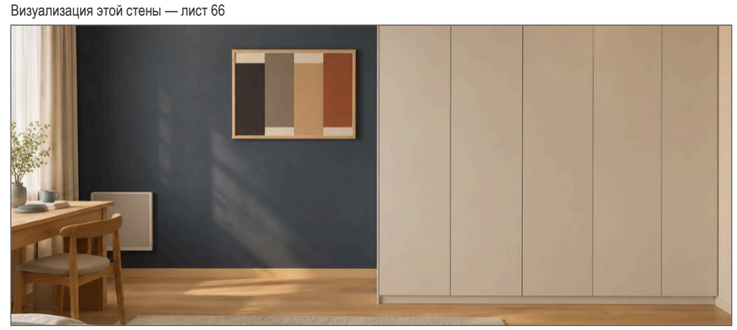

Примечания

1. Размеры — в мм от чистовых поверхностей стен; условные обозначения и общие указания — лист 2.
2. Картины и зеркала крепить к основанию по паспорту изделия (закладные и анкеры — в перечне скрытых работ); крест — ось центра предмета.

					Проект: Квартира 65 м²
	Лист	№ док.	Подпись	Дата	Развёртка стены А. Детская (пом. 9)
Дизайнер	Кырлан А.С.			21.10.26	

Стадия	Лист	Листов
П	69	80

выпуск 09.10.2026 № da691793fd · стр. 69 из 80

Правка к этому листу

Развёртка стены Б


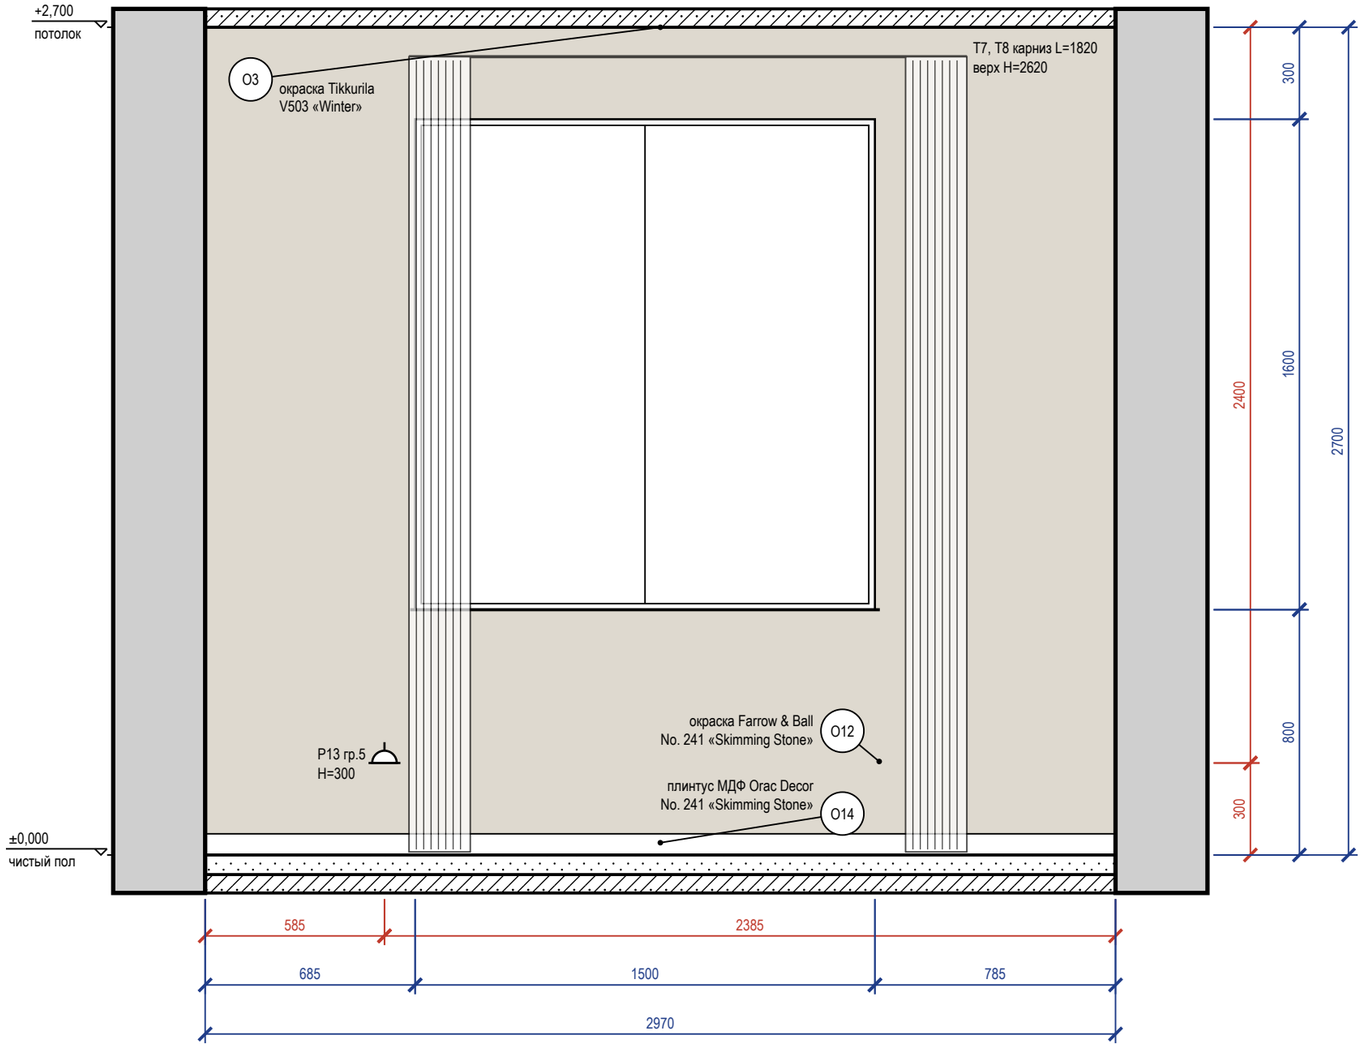


Схема развёрток (М 1:100)

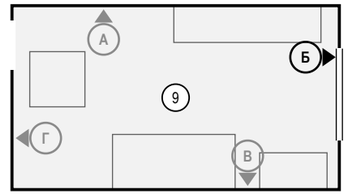

Ведомость отделки (на листе)

Марка	Поверхность	Материал, изделие	Цвет, код	Кол.
О3	потолок	окраска, Tikkurila Anti-Reflex 2, глубокоматовая, подготовка Q3	Tikkurila V503 «Winter»	16 м²
О12	стены	окраска, Farrow & Ball Modern Emulsion, матовая, подготовка Q3	Farrow & Ball No. 241 «Skimming Stone»	5,6 м²
О14	плинтус	плинтус МДФ, Orac Decor Contour (Luxxus), h 69 мм, SX165	Farrow & Ball No. 241 «Skimming Stone»	3 м

Визуализация этой стены — лист 65



Примечания

1. Размеры — в мм от чистовых поверхностей стен; условные обозначения и общие указания — лист 2.
2. Карнизы (шины) — по ведомости текстиля декоратора; длина L и верх H — по развёртке, крепление — до окраски потолка.

					Проект: Квартира 65 м²
	Лист	№ док.	Подпись	Дата	Развёртка стены Б. Детская (пом. 9)
Дизайнер	Кырлан А.С.			21.10.26	

Стадия	Лист	Листов
П	70	80

выпуск 09.10.2026 № da691793fd · стр. 70 из 80

Правка к этому листу

Развёртка стены В


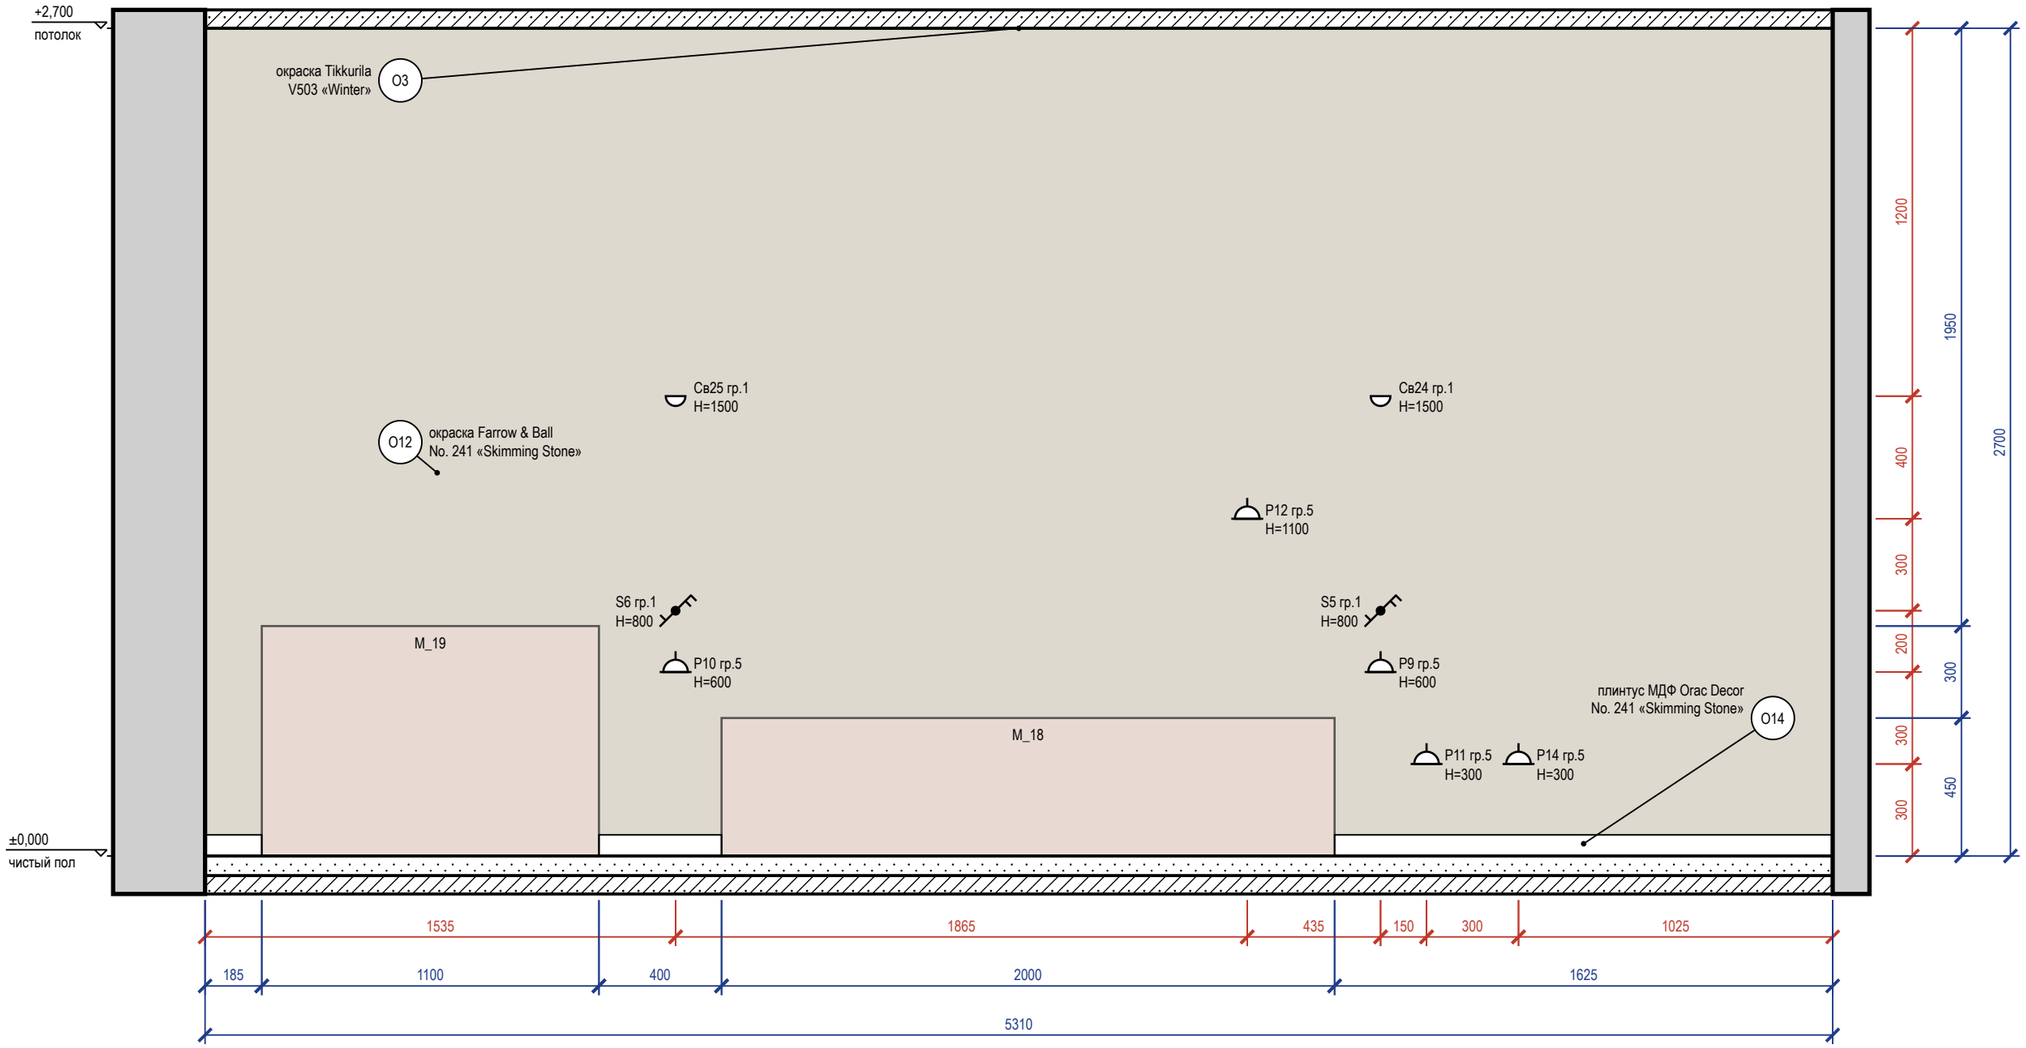


Схема развёрток (М 1:100)

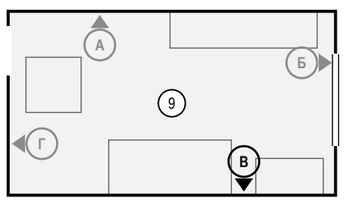

Ведомость отделки (на листе)

Марка	Поверхность	Материал, изделие	Цвет, код	Кол.
О3	потолок	окраска, Tikkurila Anti-Reflex 2, глубокоматовая, подготовка Q3	Tikkurila V503 «Winter»	16 м²
О12	стены	окраска, Farrow & Ball Modern Emulsion, матовая, подготовка Q3	Farrow & Ball No. 241 «Skimming Stone»	14,3 м²
О14	плинтус	плинтус МДФ, Orac Decor Contour (Luxxus), h 69 мм, SX165	Farrow & Ball No. 241 «Skimming Stone»	2,2 м

Визуализация этой стены — лист 67



Примечания

1. Размеры — в мм от чистовых поверхностей стен; условные обозначения и общие указания — лист 2.

					Проект: Квартира 65 м²
	Лист	№ док.	Подпись	Дата	Развёртка стены В. Детская (пом. 9)
Дизайнер	Кырлан А.С.			21.10.26	

Стадия	Лист	Листов
П	71	80

выпуск 09.10.2026 № da691793fd · стр. 71 из 80

Правка к этому листу

Развёртка стены Г


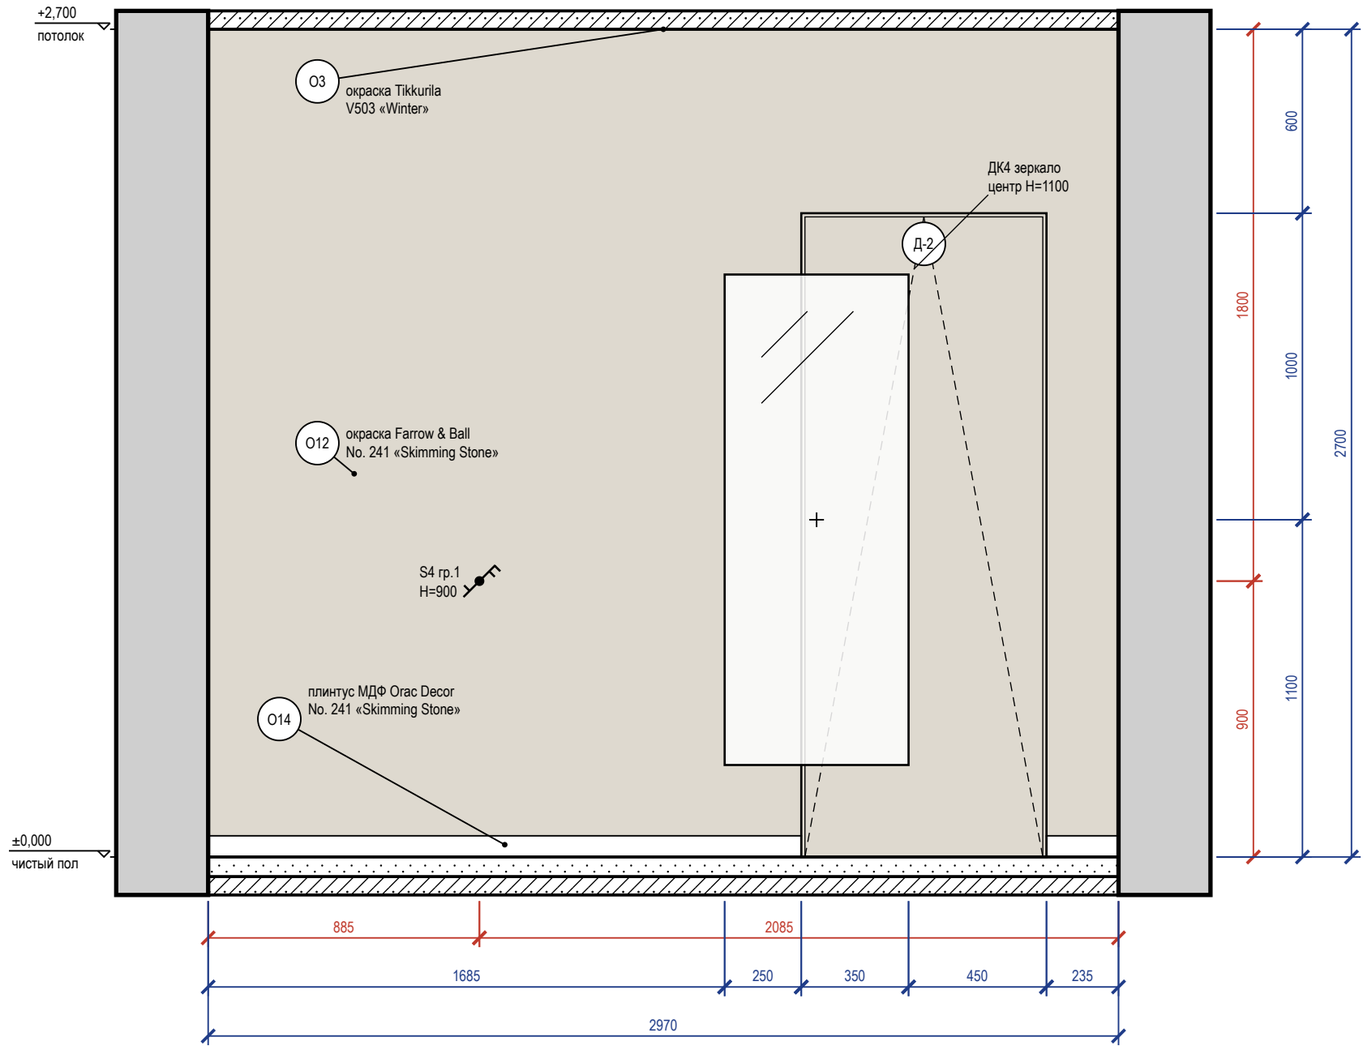


Схема развёрток (М 1:100)

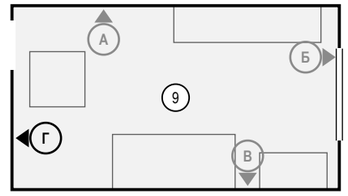

Ведомость отделки (на листе)

Марка	Поверхность	Материал, изделие	Цвет, код	Кол.
О3	потолок	окраска, Tikkurila Anti-Reflex 2, глубокоматовая, подготовка Q3	Tikkurila V503 «Winter»	16 м²
О12	стены	окраска, Farrow & Ball Modern Emulsion, матовая, подготовка Q3	Farrow & Ball No. 241 «Skimming Stone»	6,3 м²
О14	плинтус	плинтус МДФ, Orac Decor Contour (Luxxus), h 69 мм, SX165	Farrow & Ball No. 241 «Skimming Stone»	2,2 м

Визуализация этой стены — лист 68



Примечания


1. Размеры — в мм от чистовых поверхностей стен; условные обозначения и общие указания — лист 2.
2. Картины и зеркала крепить к основанию по паспорту изделия (закладные и анкеры — в перечне скрытых работ); крест — ось центра предмета.
3. Двери скрытого монтажа — полотно в плоскости стены, отделка стены по полотну, плинтус прерывается у короба (узел — на листе узлов).

					Проект: Квартира 65 м²
	Лист	№ док.	Подпись	Дата	Развёртка стены Г. Детская (пом. 9)
Дизайнер	Кырлан А.С.			21.10.26	


Стадия	Лист	Листов
П	72	80

Правка к этому листу


Общий вид

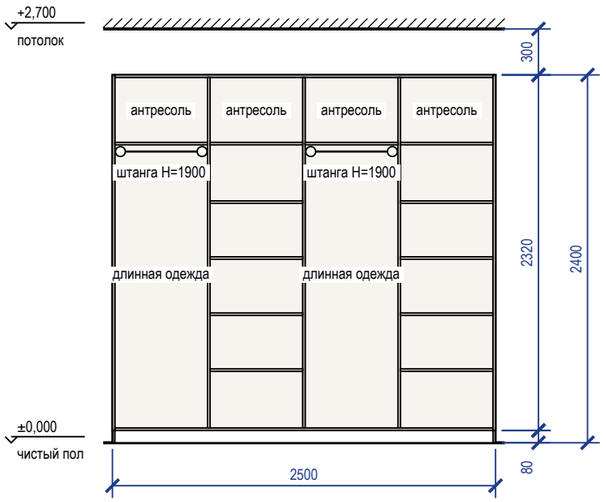


Наполнение, размеры в свету

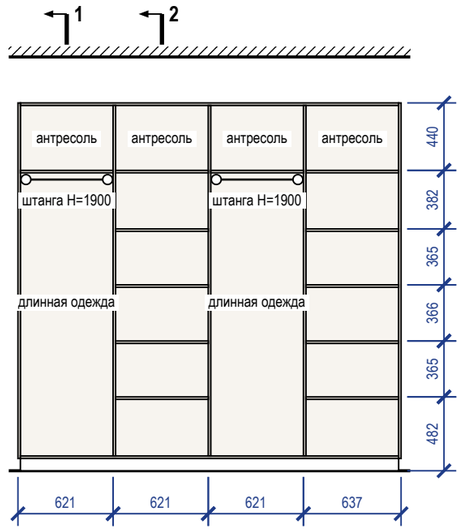

Разрез 1-1

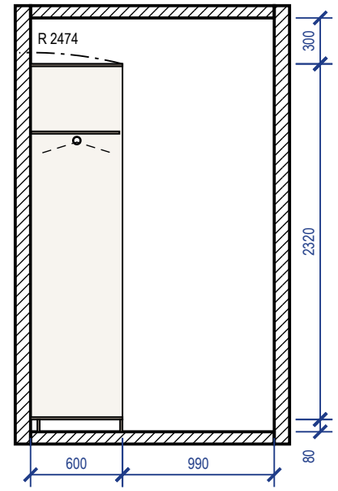


Разрез 2-2

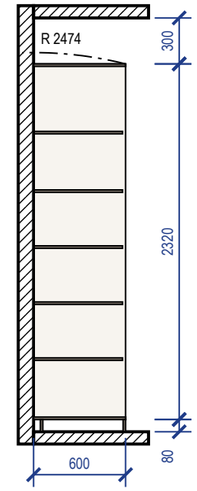

Примечания

1. Размеры — в мм по чистовой отделке; изделие 2500×600×2400 (Ш×Г×В). Перед раскроем — контрольный замер цеха после чистовой отделки стен, пола и потолка.
2. Корпус — ЛДСП 16 мм, задняя стенка ХДФ 4 мм в паз, цоколь 80 мм на регулируемых опорах; открытая система без фасадов, ящики с фасадами.
3. Кромка: скрытые торцы 0,4 мм, видимые 2 мм (ПВХ/АБС).
4. Номинальные зазоры: между фасадами ящиков 3 мм, фасад ящика — стойка 2 мм.
5. Ящики — направляющие полного выдвижения NL 550 (внутренняя глубина 596 мм ≥ NL + 3); присадка по 32-й системе — выполняет цех.
6. Зазор до потолка 300 мм.
7. Подъём корпуса: диагональ боковины $\sqrt{(2400^2 + 600^2)}$ = 2474 мм < 2700 мм до потолка — корпус собирается лёжа и поднимается поворотом.
8. Крепление к стене от опрокидывания: крепление к стене, 3 точки; основание стены и шаг анкеров — монтажная схема шкафов.
9. Проход перед изделием 990 мм показан на разрезе 1-1.

3D орто

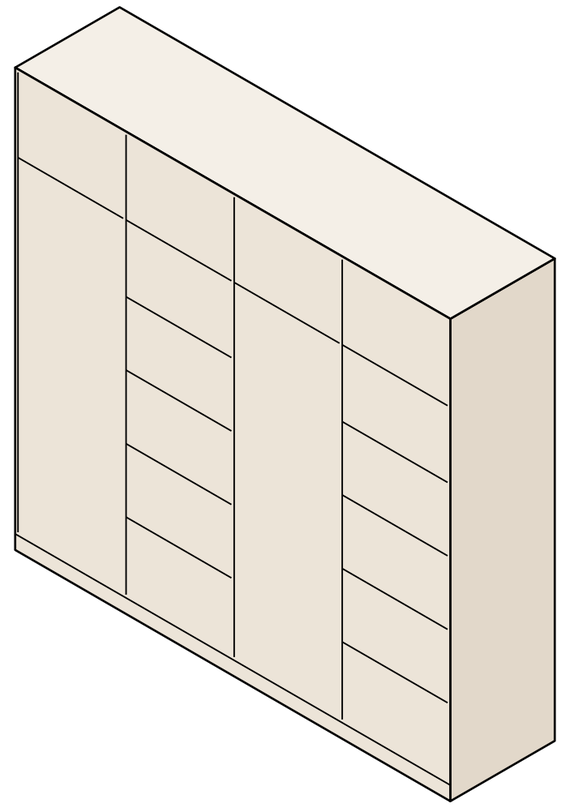


					Проект: Квартира 65 м²
	Лист	№ док.	Подпись	Дата	
Дизайнер	Кырлан А.С.			21.10.26	Система хранения M_01


Стадия	Лист	Листов
П	Д_1	80

Правка к этому листу


Вид с фасадами

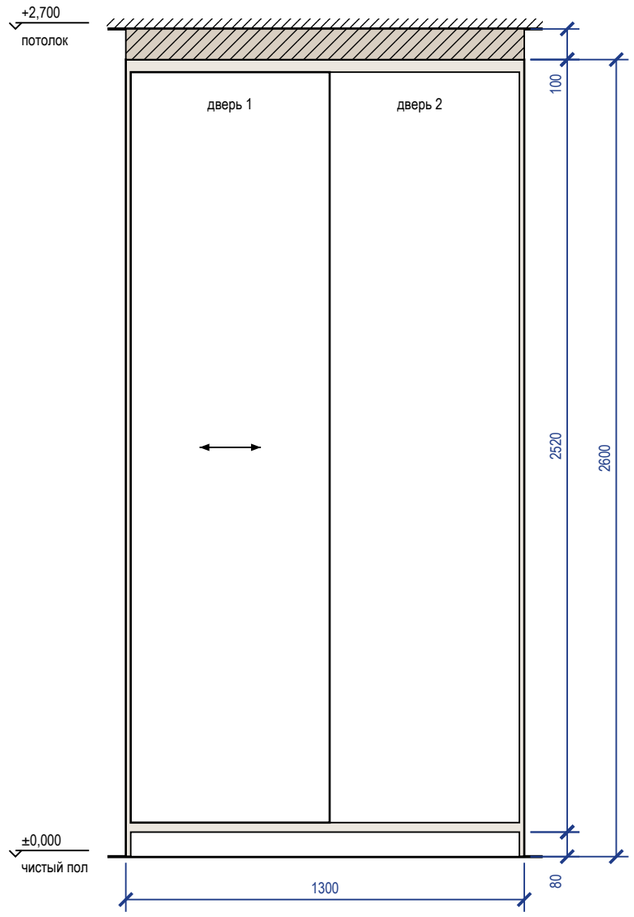


Вид без фасадов

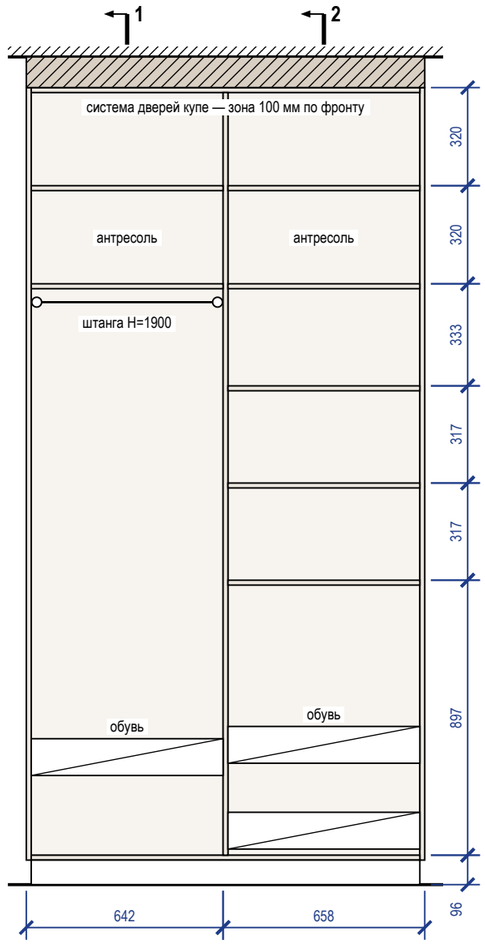

Разрез 1-1

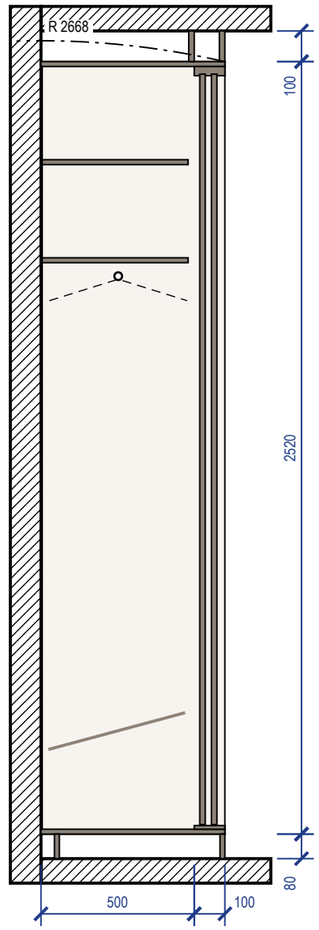


Разрез 2-2

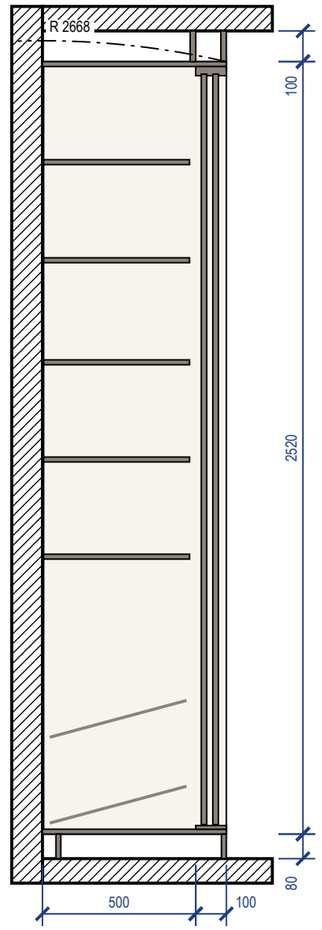

Примечания

1. Размеры — в мм по чистовой отделке; изделие 1300×600×2600 (Ш×Г×В). Перед раскроем — контрольный замер цеха после чистовой отделки стен, пола и потолка.
2. Корпус — ЛДСП 16 мм, задняя стенка ХДФ 4 мм в паз, цоколь 80 мм на регулируемых опорах; двери купе — ЛДСП 10 мм в алюминиевом профиле, нахлёст 30 мм, ширина двери 649 мм, высота — проём минус 40 мм; цвет — по колерной карте.
3. Кромка: скрытые торцы 0,4 мм, видимые 1 мм (ПВХ/АБС).
4. Номинальные зазоры: дверь купе — боковина 3 мм, фасад ящика — стойка 2 мм; ящики внутри купе — с накладкой 30 мм на стойке со стороны нахлёста дверей.
5. Ящики — направляющие полного выдвижения NL 450 (внутренняя глубина 496 мм ≥ NL + 3); присадка по 32-й системе — выполняет цех.
6. Компенсатор 100 мм — короб из ЛДСП по фронту и торцам, подгоняется к потолку при монтаже (припуск 20 мм), крепится к корпусу и к потолку.
7. Подъём корпуса: диагональ боковины $\sqrt{(2600^2 + 600^2)} = 2668$ мм < 2700 мм до потолка — корпус собирается лёжа и поднимается поворотом.
8. Крепление к стене от опрокидывания — уголки 2 шт. к несущему основанию (монтажная схема шкафов).

3D орто

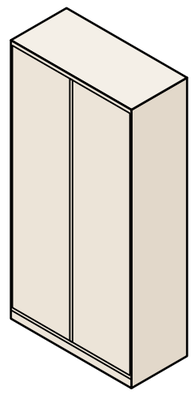


					Проект: Квартира 65 м²
	Лист	№ док.	Подпись	Дата	Шкаф-купе M_15
Дизайнер	Кырлан А.С.			21.10.26	


Стадия	Лист	Листов
П	Д_2	80

Правка к этому листу


Общий вид

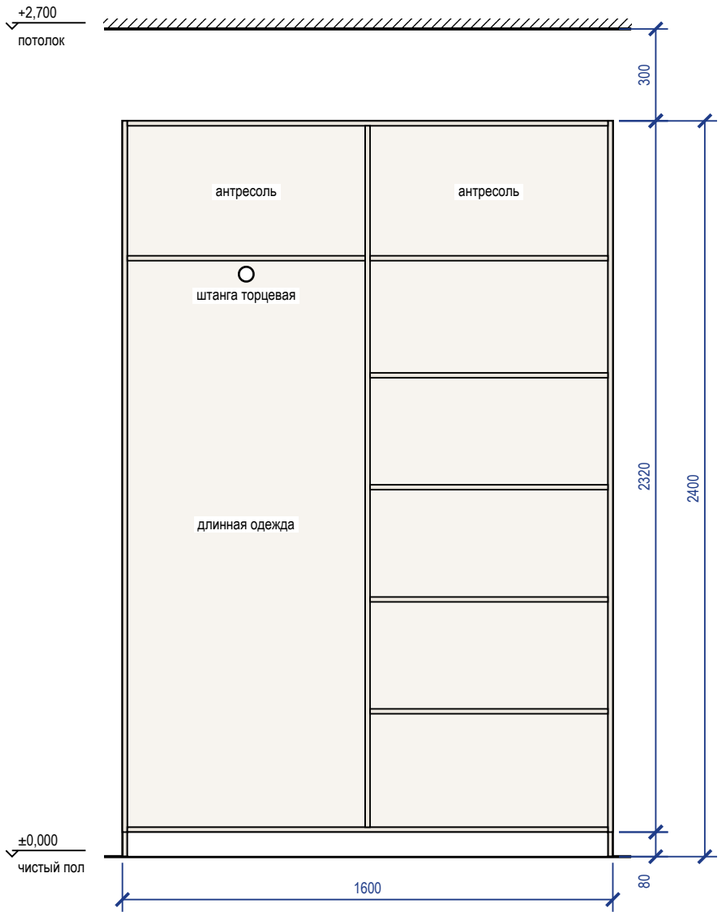


Наполнение, размеры в свету

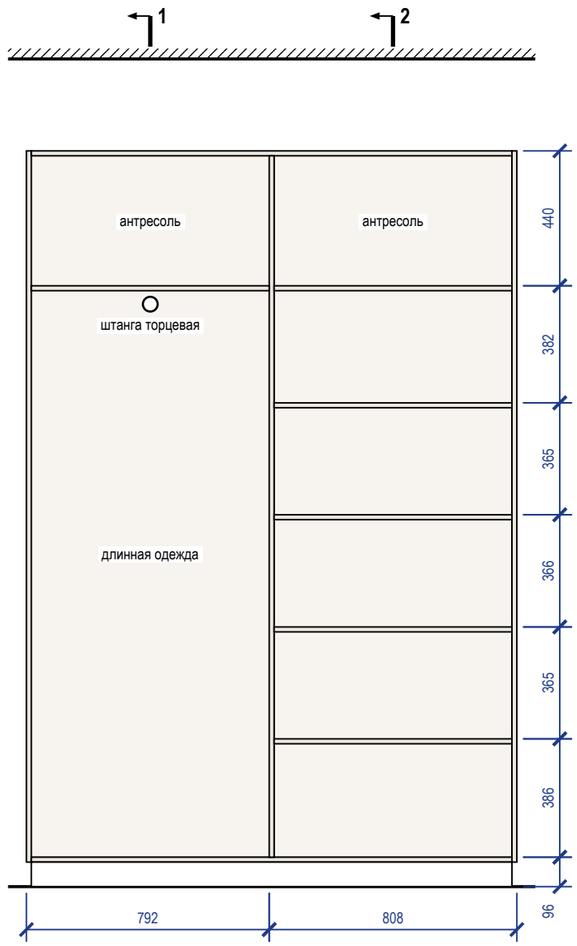

Разрез 1-1

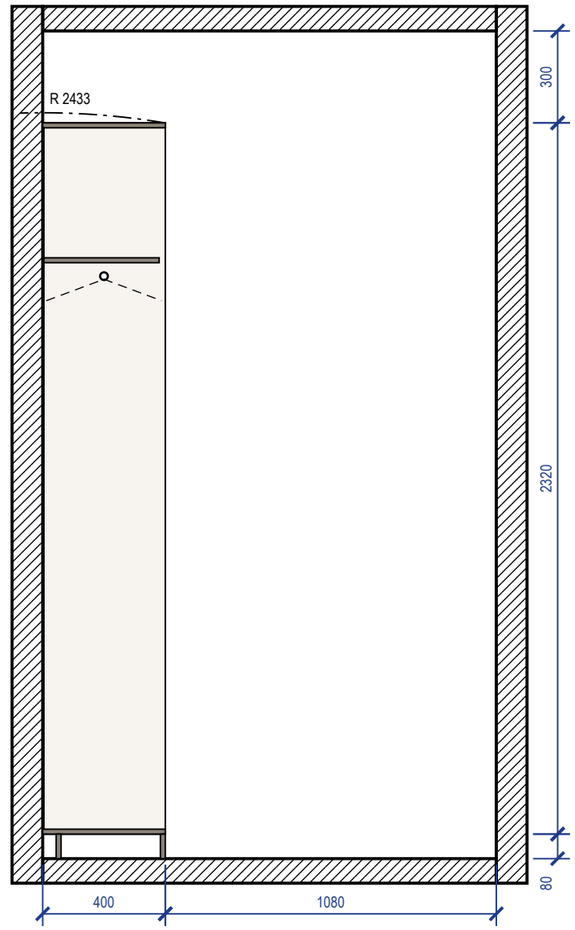


Разрез 2-2

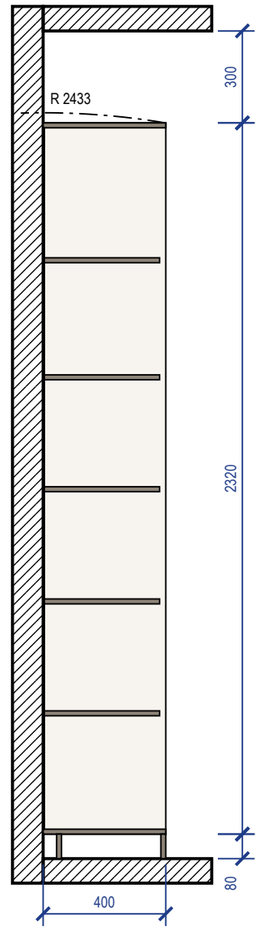

Примечания

1. Размеры — в мм по чистовой отделке; изделие 1600×400×2400 (Ш×Г×В). Перед раскроем — контрольный замер цеха после чистовой отделки стен, пола и потолка.
2. Корпус — ЛДСП 16 мм, задняя стенка ХДФ 4 мм в паз, цоколь 80 мм на регулируемых опорах; открытая система без фасадов, ящики с фасадами.
3. Кромка: скрытые торцы 0,4 мм, видимые 2 мм (ПВХ/АБС).
4. Номинальные зазоры: между фасадами ящиков 3 мм, фасад ящика — стойка 2 мм.
5. Ящики — направляющие полного выдвижения NL 350 (внутренняя глубина 396 мм ≥ NL + 3); присадка по 32-й системе — выполняет цех.
6. Зазор до потолка 300 мм.
7. Подъём корпуса: диагональ боковины $\sqrt{(2400^2 + 400^2)} = 2433$ мм < 2700 мм до потолка — корпус собирается лёжа и поднимается поворотом.
8. Крепление к стене от опрокидывания — уголки 2 шт. к несущему основанию (монтажная схема шкафов).
9. Проход перед изделием 1080 мм показан на разрезе 1-1.

3D орто

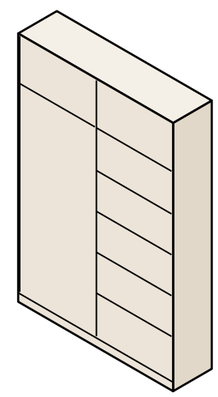


					Проект: Квартира 65 м²		
	Лист	№ док.	Подпись	Дата	Система хранения M_16	Стадия	Лист	Листов
Дизайнер	Кырлан А.С.			21.10.26		П	Д_3	80


выпуск 09.10.2026 № da691793fd · стр. 75 из 80

Правка к этому листу


Вид с фасадами

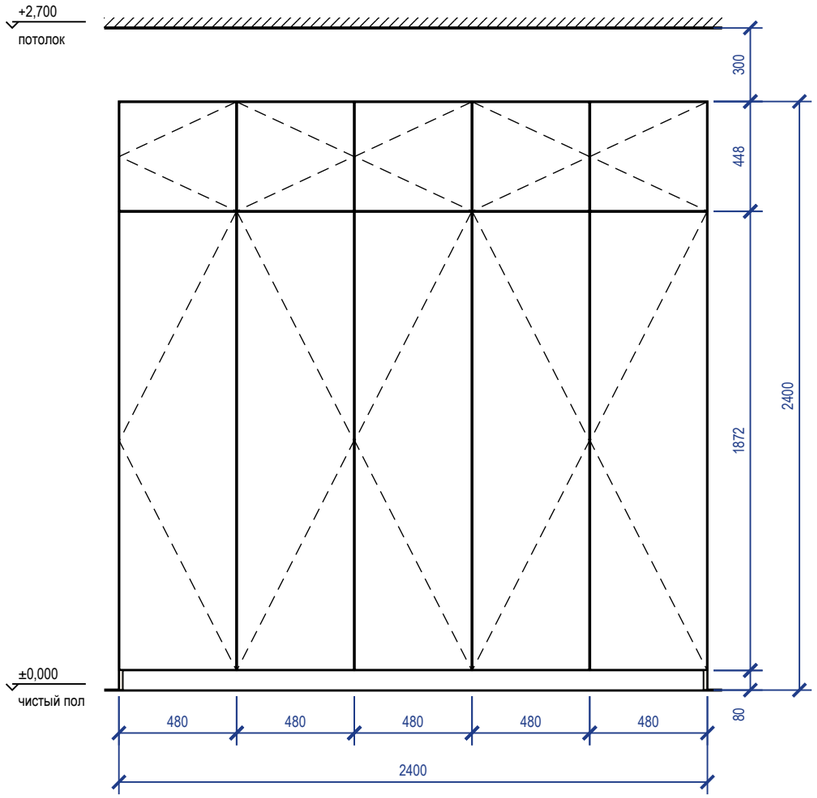


Вид без фасадов

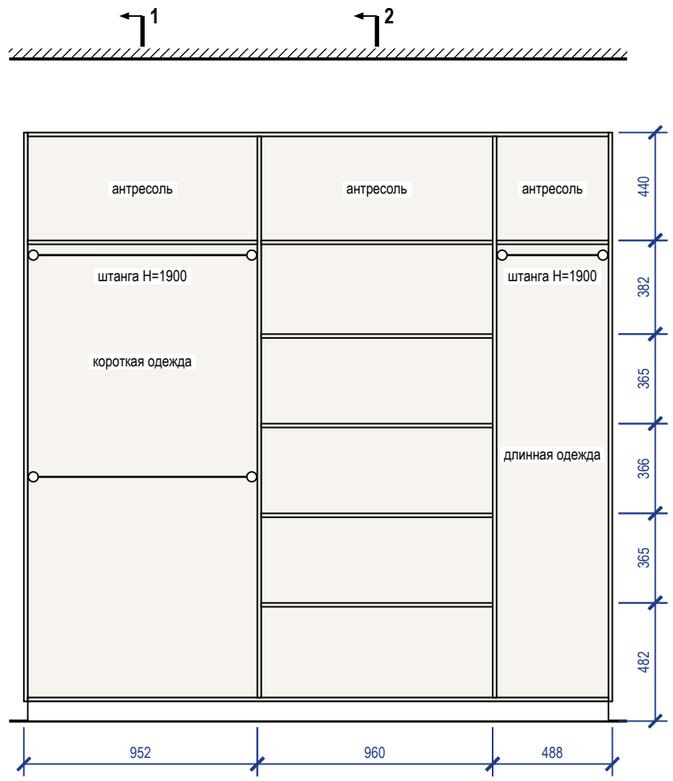

Разрез 1-1

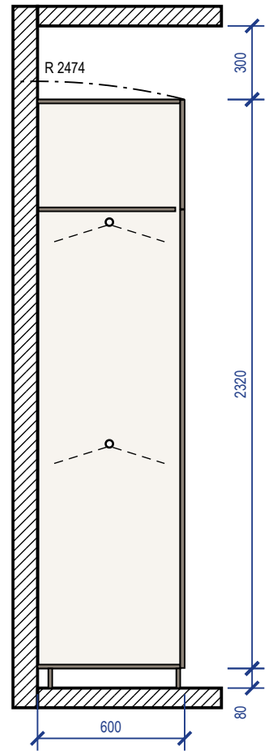


Разрез 2-2

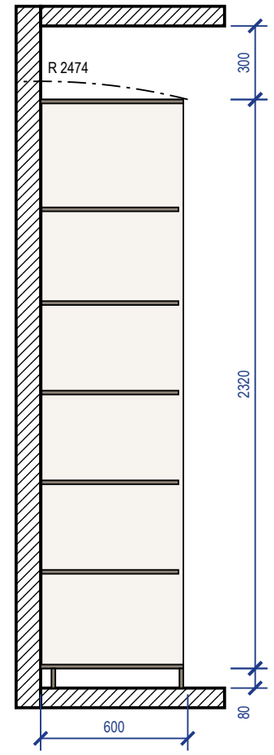

Примечания

1. Размеры — в мм по чистовой отделке; изделие 2400×600×2400 (Ш×Г×В). Перед раскроем — контрольный замер цеха после чистовой отделки стен, пола и потолка.
2. Корпус — ЛДСП 16 мм, задняя стенка ХДФ 4 мм в паз, цоколь 80 мм на регулируемых опорах; фасады — МДФ, эмаль матовая 18 мм накладные, цвет — по колерной карте; петли с доводчиком: фасад 1869 мм — 4 петли, фасад 445 мм — 2 петли.
3. Кромка: скрытые торцы 0,4 мм, видимые 2 мм (ПВХ/АБС).
4. Номинальные зазоры: между фасадами 3 мм, фасад — стена и фасад — потолок не менее 3 мм, фасад ящика — стойка 2 мм.
5. Ящики — направляющие полного выдвижения NL 550 (внутренняя глубина 578 мм ≥ NL + 3); присадка по 32-й системе — выполняет цех.
6. Зазор до потолка 300 мм.
7. Подъём корпуса: диагональ боковины $\sqrt{(2400^2 + 600^2)}$ = 2474 мм < 2700 мм до потолка — корпус собирается лёжа и поднимается поворотом.
8. Крепление к стене от опрокидывания — уголки 2 шт. к несущему основанию (монтажная схема шкафов).

3D орто

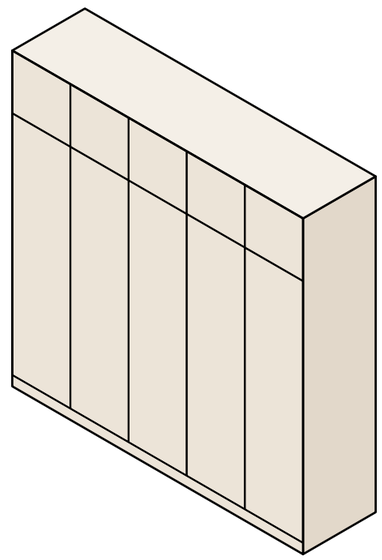


					Проект: Квартира 65 м²
	Лист	№ док.	Подпись	Дата	
Дизайнер	Кырлан А.С.			21.10.26	Шкаф распашной М_17


Стадия	Лист	Листов
П	Д_4	80

Правка к этому листу


Вид с фасадами

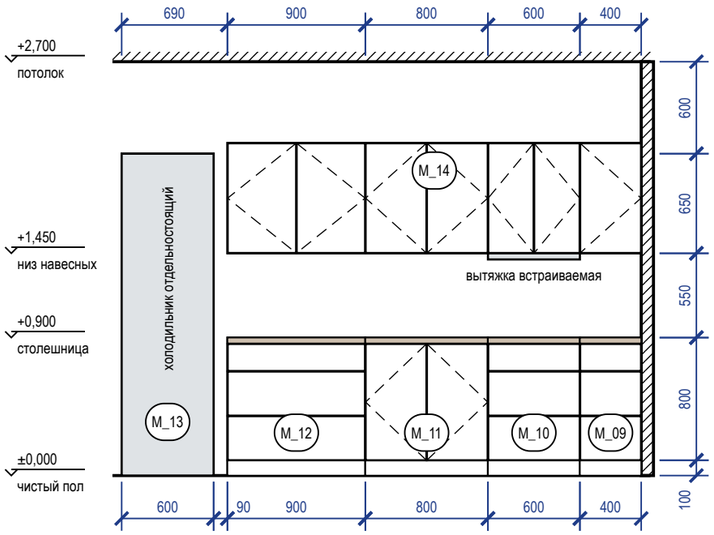


Вид без фасадов (наполнение, выводы)

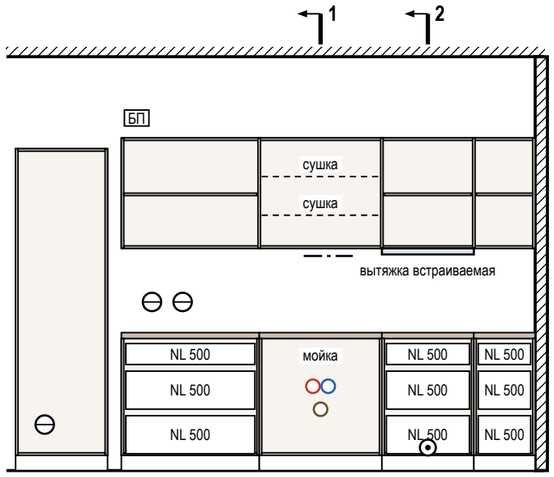


Разрез 1-1

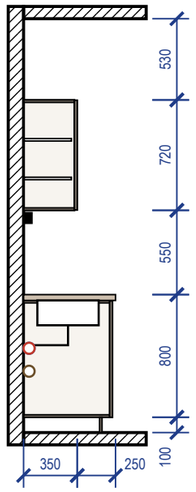

Разрез 2-2

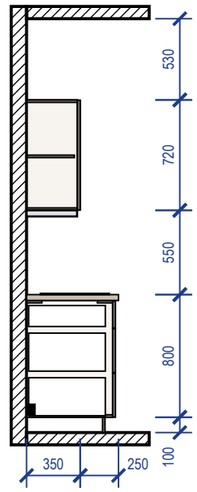

3D орто

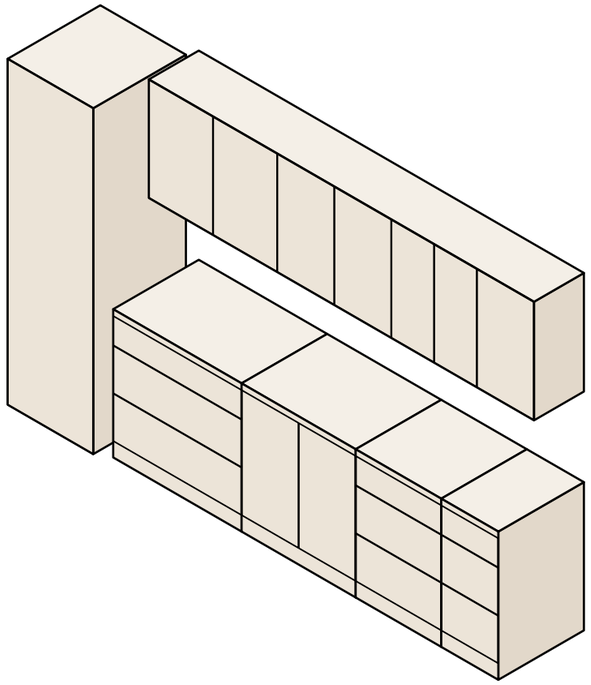

Примечания

1. Размеры — в мм по чистовой отделке, вид из помещения; марки — как на плане расстановки. Перед раскроем — контрольный замер цеха после фартука и пола.
2. Корпуса — ЛДСП 16 мм, задняя стенка ХДФ 4 мм; фасады — МДФ эмаль 18 мм, цвет по колерной карте; столешница 38 мм, свес 20 мм; цоколь 100 мм.
3. Кромка: скрытые торцы 0,4 мм, видимые 1 мм. Номинальные зазоры: между фасадами 3 мм, фасад — столешница 3 мм, фасад — стена не менее 3 мм.
4. Ящики полного выдвижения и петли — с доводчиком; присадка по 32-й системе — выполняет цех.
5. Вытяжка встраивается в навесной модуль над варочной: её низ 510 мм над панелью — меньше 650 мм, модуль поднять или принять вытяжку с допуском по паспорту модели.
6. Ниши техники — по монтажным схемам выбранных моделей: решётка в цоколе и канал за пеналом холодильника, зазор за духовым шкафом, фасад ПММ на двери машины.

					Проект: Квартира 65 м²
	Лист	№ док.	Подпись	Дата	Кухня (пом. 3). Развёртка гарнитура
Дизайнер	Кырлан А.С.			21.10.26	

Стадия	Лист	Листов
П	Д_5	80

выпуск 09.10.2026 № da691793fd · стр. 77 из 80

Ведомость отделки помещений (форма 1 прил. А ГОСТ 21.501-2018)

№	Наименование помещения	Потолок			Стены и перегородки			Низ стен (плинтус)			Пол		Примечание
		Вид отделки	Код цвета	S, м²	Вид отделки	Код цвета	S, м²	Вид отделки	Код цвета	L, м	Вид отделки	S, м²	
1	Гардеробная 4,20 м²	Окраска, Tikkurila Anti-Reflex 2, глубокоматовая, 2 слоя, подготовка Q3	Tikkurila V503	4,20	Окраска, Tikkurila Harmony, матовая, 2 слоя, подготовка Q3	Tikkurila V503	21,37	Плинтус МДФ h=69 мм, SX165	Tikkurila V503	7,8	Инженерная доска, IM1848, 1380×190 мм, на клею; тип 1, отм. ЧП ±0,000	4,20	Н стен 2700 (до потолка); плинтус в цвет: стены
2	Спальня 8,27 м²	Окраска, Tikkurila, глубокоматовая	NCS S 0300-N	8,27	Окраска, Tikkurila, глубокоматовая, подготовка Q3	NCS S 1502-Y50R	28,54	Плинтус МДФ h=69 мм, SX165	NCS S 0300-N	10,3	Инженерная доска, IM1848, 1380×190 мм, на клею; тип 2, отм. ЧП ±0,000	8,27	Н стен 2700 (до потолка)
3	Кухня-гостиная 18,91 м²	Окраска, Tikkurila, глубокоматовая	NCS S 0300-N	18,91	Окраска, Tikkurila, полуматовая, подготовка Q3	NCS S 1002-Y50R	48,29	Плинтус МДФ h=69 мм, SX165	NCS S 0300-N	18,6	Инженерная доска, IM1848, 1380×190 мм, на клею; тип 2, отм. ЧП ±0,000	18,91	Н стен 2700 (до потолка)
4	Прихожая 4,15 м²	Окраска, Tikkurila, глубокоматовая	NCS S 0300-N	4,15	Окраска, Tikkurila, полуматовая, подготовка Q3	NCS S 1502-Y50R	17,41	Плинтус МДФ h=69 мм, SX165	NCS S 0300-N	6,0	Керамогранит, SG501600R, 600×1200 мм; тип 3, отм. ЧП ±0,000	4,15	Н стен 2700 (до потолка)
5	Коридор 5,51 м²	Окраска, Tikkurila, глубокоматовая	NCS S 0300-N	5,51	Окраска, Tikkurila, полуматовая, подготовка Q3	NCS S 1502-Y50R	21,78	Плинтус МДФ h=69 мм, SX165	NCS S 0300-N	7,0	Керамогранит, SG501600R, 600×1200 мм; тип 3, отм. ЧП ±0,000	5,51	Н стен 2700 (до потолка)
6	Санузел 1,83 м²	Окраска, Tikkurila, глубокоматовая	NCS S 0300-N	1,83	Облицовка плиткой, 610010001195, 600×1200 мм, клей С2	Italon 610010001195	13,89	нет (облицовка от пола)			Керамогранит, SG501600R, 600×1200 мм; тип 4, отм. ЧП −0,015	1,83	Н стен 2715 (до потолка); гидроизоляция обмазочная, 2 слоя, с заведением на стены 200 мм (по пирогу пола); тест проливом и акт скрытых работ
7	Ванная 3,85 м²	Окраска, Tikkurila, глубокоматовая	NCS S 0300-N	3,85	Облицовка плиткой, 610010001195, 600×1200 мм, клей С2	Italon 610010001195	20,09	нет (облицовка от пола)			Керамогранит, SG501600R, 600×1200 мм; тип 4, отм. ЧП −0,015	3,85	Н стен 2715 (до потолка); тёплый пол; гидроизоляция обмазочная, 2 слоя, с заведением на стены 200 мм (по пирогу пола); тест проливом и акт скрытых работ
8	Кладовая 2,50 м²	Окраска, Tikkurila, глубокоматовая	NCS S 0300-N	2,50	Окраска, Tikkurila, матовая, подготовка Q3	NCS S 0502-Y	15,65	Плинтус МДФ h=69 мм, SX165	NCS S 0300-N	5,6	Инженерная доска, IM1848, 1380×190 мм, на клею; тип 2, отм. ЧП ±0,000	2,50	Н стен 2700 (до потолка)
9	Детская 16,02 м²	Окраска, Tikkurila Anti-Reflex 2, глубокоматовая, 2 слоя, подготовка Q3	Tikkurila V503	16,02	Окраска, Farrow & Ball Modern Emulsion, матовая, 2 слоя, подготовка Q3 Акцент — стена А: окраска, Farrow & Ball Modern Emulsion, матовая, 2 слоя, подготовка Q3	Farrow & Ball No. 241 Farrow & Ball No. 30	26,54 14,42	Плинтус МДФ h=69 мм, SX165	Farrow & Ball No. 241	15,9	Инженерная доска, IM1848, 1380×190 мм, на клею; тип 1, отм. ЧП ±0,000	16,02	Н стен 2700 (до потолка); плинтус в цвет: стены
	Итого			**65,24**			**227,98**			**71,1**		**65,24**	

Сводка площадей по материалам отделки

Поверхность	Материал / код цвета	Серия	Площадь, м²
Потолок	Tikkurila V503	Anti-Reflex 2	20,22
Потолок	NCS S 0300-N		45,02
Стены	Tikkurila V503	Harmony	21,37
Стены	NCS S 1502-Y50R		67,74
Стены	NCS S 1002-Y50R		48,29
Стены	облицовка плиткой 600×1200 мм, Italon 610010001195	610010001195	33,97
Стены	NCS S 0502-Y		15,65
Стены	Farrow & Ball No. 241	Modern Emulsion	26,54
Стены	Farrow & Ball No. 30	Modern Emulsion	14,42

Примечания

1. Площади поверхностей — по чистым граням стен до отделки: стены = периметр × высоту от чистого пола помещения до низа потолка минус проёмы (облицовка плиткой — до верха облицовки); плинтус = периметр минус дверные проёмы; пол и потолок — по площади помещения. Количество плиток по раскладке. Площади помещений — с учётом всех частей помещения; откосы в площадь стен не входят.
2. Акцентные стены — отдельными строками, их площадь вычтена из основной отделки стен помещения.
3. Плинтус — длина по периметру за вычетом дверных проёмов; примыкания к наличникам и встроенной мебели — по развёрткам.
4. Формат плитки — Ш×В×Т (ширина × высота в положении укладки × толщина), мм; на полу — вдоль стен А/В × вдоль стен Б/Г.
5. Коды цвета — по веерам производителей; колеровка каждой краски одной партией, проверка выкраса при свете D65 и при лампах проекта.
6. Уровни подготовки Q1–Q4 — система Knauf, не норма ГОСТ/СП; допуски поверхностей — по СП 71.13330.2017 (действующая редакция).
7. «аналог:» — изделие задано характеристиками, марку и артикул согласовать с заказчиком до закупки.

					Проект: Квартира 65 м²			
	Лист	№ док.	Подпись	Дата	Ведомость отделки помещений	Стадия	Лист	Листов
Дизайнер	Кырлан А.С.			21.10.26		П	С1	80

Правка к этому листу

Поз.	Наименование и техническая характеристика	Тип, марка, обозначение документа	Код продукции	Поставщик	Ед. изм.	Кол.	Образец	Примечание
	Лакокрасочные материалы							
1	Краска интерьерная водно-дисперсионная акриловая для стен, матовая, класс мокрого истирания 1 по EN 13300, база A; цвет Tikkurila V503 «Winter», колеровка машинная	Tikkurila Harmony		Tikkurila	л	6,3		поз. К1 колерной карты; пом. 1; S = 21,4 м² × 2 сл. × 0,12 л/м² = 5,1 л, +10 % и 0,5 л на подкраску → ≥ 6,1 л; тара 2 × 2,7 л + 1 × 0,9 л
2	Краска интерьерная водно-дисперсионная акриловая для потолков, глубокоматовая, класс мокрого истирания 2 по EN 13300, база A; цвет Tikkurila V503 «Winter», колеровка машинная	Tikkurila Anti-Reflex 2		Tikkurila	л	6,3		поз. К2 колерной карты; пом. 1, 9; S = 20,2 м² × 2 сл. × 0,12 л/м² = 4,9 л, +10 % и 0,5 л на подкраску → ≥ 5,8 л; тара 2 × 2,7 л + 1 × 0,9 л
3	Краска интерьерная водно-дисперсионная акриловая для стен, глубокоматовая, класс мокрого истирания 2 по EN 13300, база A; цвет NCS S 1502-Y50R, колеровка машинная	Tikkurila		Tikkurila	л	8,1		поз. К4 колерной карты; пом. 2; S = 28,5 м² × 2 сл. × 0,12 л/м² = 6,9 л, +10 % и 0,5 л на подкраску → ≥ 8,0 л; тара 3 × 2,7 л
4	Краска интерьерная водно-дисперсионная для потолков, глубокоматовая, класс мокрого истирания 2 по EN 13300, база A; цвет NCS S 0300-N, колеровка машинная	Tikkurila		Tikkurila	л	3,6		поз. К5 колерной карты; пом. 2, 8; S = 10,8 м² × 2 сл. × 0,12 л/м² = 2,6 л, +10 % и 0,5 л на подкраску → ≥ 3,3 л; тара 1 × 2,7 л + 1 × 0,9 л
5	Краска интерьерная водно-дисперсионная акриловая для стен, полуматовая, класс мокрого истирания 1 по EN 13300, база A; цвет NCS S 1002-Y50R, колеровка машинная	Tikkurila		Tikkurila	л	13,5		поз. К7 колерной карты; пом. 3; S = 48,3 м² × 2 сл. × 0,12 л/м² = 11,6 л, +10 % и 0,5 л на подкраску → ≥ 13,2 л; тара 1 × 9 л + 1 × 2,7 л + 2 × 0,9 л
6	Краска интерьерная водно-дисперсионная для потолков, глубокоматовая, класс мокрого истирания 1 по EN 13300, база A; цвет NCS S 0300-N, колеровка машинная	Tikkurila		Tikkurila	л	9,9		поз. К8 колерной карты; пом. 3, 4, 5, 6, 7; S = 34,3 м² × 2 сл. × 0,12 л/м² = 8,2 л, +10 % и 0,5 л на подкраску → ≥ 9,5 л; тара 1 × 9 л + 1 × 0,9 л
7	Краска интерьерная водно-дисперсионная акриловая для стен, полуматовая, класс мокрого истирания 1 по EN 13300, база A; цвет NCS S 1502-Y50R, колеровка машинная	Tikkurila		Tikkurila	л	11,7		поз. К9 колерной карты; пом. 4, 5; S = 39,2 м² × 2 сл. × 0,12 л/м² = 9,4 л, +10 % и 0,5 л на подкраску → ≥ 10,8 л; тара 1 × 9 л + 1 × 2,7 л
8	Краска интерьерная водно-дисперсионная акриловая для стен, матовая, класс мокрого истирания 2 по EN 13300, база A; цвет NCS S 0502-Y, колеровка машинная	Tikkurila		Tikkurila	л	5,4		поз. К12 колерной карты; пом. 8; S = 15,6 м² × 2 сл. × 0,12 л/м² = 3,8 л, +10 % и 0,5 л на подкраску → ≥ 4,6 л; тара 2 × 2,7 л
9	Краска интерьерная водно-дисперсионная акриловая для стен, матовая, класс мокрого истирания 1 по EN 13300, база A; цвет Farrow & Ball No. 241 «Skimming Stone», колеровка машинная	Farrow & Ball Modern Emulsion		Farrow & Ball	л	10		поз. К13 колерной карты; пом. 9; S = 26,5 м² × 2 сл. × 0,12 л/м² = 6,4 л, +10 % и 0,5 л на подкраску → ≥ 7,5 л; тара 2 × 5 л
10	Краска интерьерная водно-дисперсионная акриловая для акцентных стен, матовая, класс мокрого истирания 1 по EN 13300, база C; цвет Farrow & Ball No. 30 «Hague Blue», колеровка машинная	Farrow & Ball Modern Emulsion		Farrow & Ball	л	5		поз. К14 колерной карты; пом. 9; S = 14,4 м² × 2 сл. × 0,12 л/м² = 3,5 л, +10 % и 0,5 л на подкраску → ≥ 4,3 л; тара 1 × 5 л
11	Краска для МДФ и дерева в цвет Tikkurila V503 «Winter» — окраска плинтуса; блеск не ниже блеска стен	марка не задана			л	0,5		поз. К3; пом. 1; L = 7,8 м, S = 0,7 м² × 2 сл. × 0,12 л/м² + 10 %; продукт подобрать в веере Tikkurila
12	Акрил, полуматовая в цвет NCS S 0300-N — окраска плинтуса	аналог по характеристикам			л	1,1		поз. К6; пом. 2, 3, 4, 5, 8; L = 47,4 м, S = 4,0 м² × 2 сл. × 0,12 л/м² + 10 %; продукт подобрать в веере NCS
13	Краска для МДФ и дерева в цвет Farrow & Ball No. 241 «Skimming Stone» — окраска плинтуса; блеск не ниже блеска стен	марка не задана			л	0,5		поз. К15; пом. 9; L = 15,9 м, S = 1,3 м² × 2 сл. × 0,12 л/м² + 10 %; продукт подобрать в веере Farrow & Ball
14	Грунтовка акриловая под окраску стен и потолков — из системы производителя краски	по системе краски			м²	260		площадь окраски стен, акцентов и потолков; 1 слой перед окраской; расход — по ТУ грунтовки
	Плитка и керамогранит							
15	SG501600R, 600×1200 мм, противоскольжение R10	SG501600R		Kerama Marazzi	м²	23,04		шов 2 мм; Прихожая, пол; Коридор, пол; Санузел, пол; Ванная, пол; по раскладке 28 шт (S = 15,34 м²), с запасом 32 шт
16	610010001195, 600×1200 мм	610010001195		Italon	м²	15,28		6. Санузел, стены; раскладка не выполнена — S = 13,89 м² + 10 %; клей и затирка — по раскладке
17	610010001195, 600×1200 мм	610010001195		Italon	м²	22,10		7. Ванная, стены; раскладка не выполнена — S = 20,09 м² + 10 %; клей и затирка — по раскладке
	Напольные покрытия							
18	IM1848, рабочий слой 4 мм, эмиссия E1, укладка на клей	IM1848		Quick-Step	м²	21,7		пом. 1, 9; S = 20,22 м² + 7 % (прямая укладка); к заказу — кратно упаковке
19	IM1848, класс 33, рабочий слой 4 мм, эмиссия E1, укладка на клей	IM1848		Quick-Step	м²	31,8		пом. 2, 3, 8; S = 29,68 м² + 7 % (прямая укладка); к заказу — кратно упаковке
20	Клей для паркета и инженерной доски, эластичный (СМП / полиуретановый)	по рекомендации производителя доски			м²	50		площадь приклейки; расход и шпатель — по ТУ клея
	Погонажные изделия							
21	SX165, h = 69 мм, крепление к стене, окраска в цвет Tikkurila V503	SX165		Orac Decor	м	79		пом. 1, 2, 3, 4, 5, 8, 9; L = 71,1 м (периметр без дверных проёмов) + 10 % на подрезку; в штуках — по длине планки
	Смеси и материалы для облицовки							
22	Затирка для швов плитки	аналог по характеристикам			кг	1,2		по раскладке (a+b)/(a·b) × шов × t × 1,6 + 10 %
23	Клей плиточный C2 по EN 12004, слой 5 мм	аналог по характеристикам			кг	79		4 меш. по 25 кг; 1,5 кг/м² на 1 мм слоя + 10 %
24	Клей плиточный C2 S1 по EN 12004, слой 5 мм	аналог по характеристикам			кг	46		2 меш. по 25 кг; 1,5 кг/м² на 1 мм слоя + 10 %
25	Лента демпферная по периметру пола из плитки	аналог по характеристикам			м	27,2		периметр без дверных проёмов + 10 %

Примечания

1. Количества — из геометрии проекта: площади поверхностей по чистым граням стен до отделки (те же, что в ведомости отделки и колерной карте), плитка, клей и затирка — по раскладке плиточника; в графе «Кол.» — к заказу, с запасом.
2. Краска: расход 0,12 л/м² на слой в 2 слоя, если по ТУ не задан иной; запас 10 % и 0,5 л на подкраску каждого кода. Один код — одна партия, колеровка машинная в колеровочном центре бренда; в заказ — только после утверждения выкраса (колерная карта). Фасовка — по каталогу бренда на дату выпуска; к заказу — не меньше расчётного объёма.
3. «Аналог по характеристикам» — допускается изделие другого производителя с характеристиками не ниже указанных, по согласованию с автором проекта.
4. Графы «Код продукции» и «Масса 1 ед.» не заполнены: коды по классификатору продукции не присвоены, масса единицы до 25 кг (ГОСТ 21.110-2013).
5. Грунтовка и клей для доски указаны площадью обработки; объём — по ТУ выбранного продукта.

	Лист	№ док.	Подпись	Дата
Дизайнер	Кырлан А.С.			21.10.26

Проект: Квартира 65 м²


Спецификация отделочных материалов

Стадия	Лист	Листов
П	С2	80

Правка к этому листу


1 Порог 15 мм: мокрая зона — жилое помещение (М 1:5)

Применение: двери Д-4

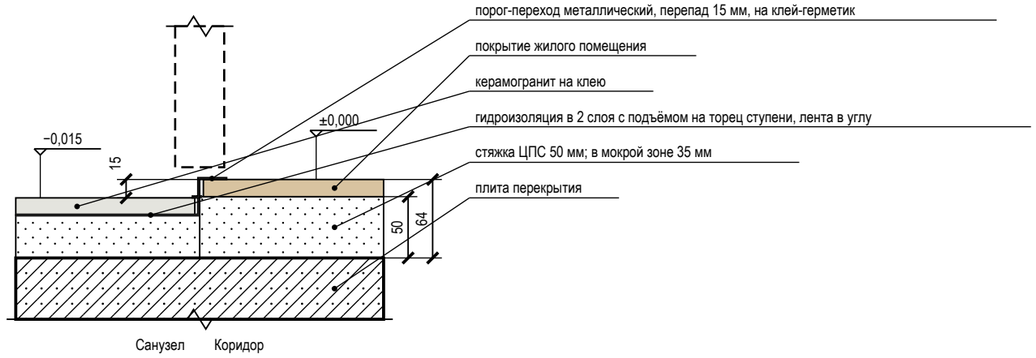


2 Дверь скрытого монтажа в плоскости стены, плинтус (М 1:5)

Применение: двери Д-3, Д-2, Д-4

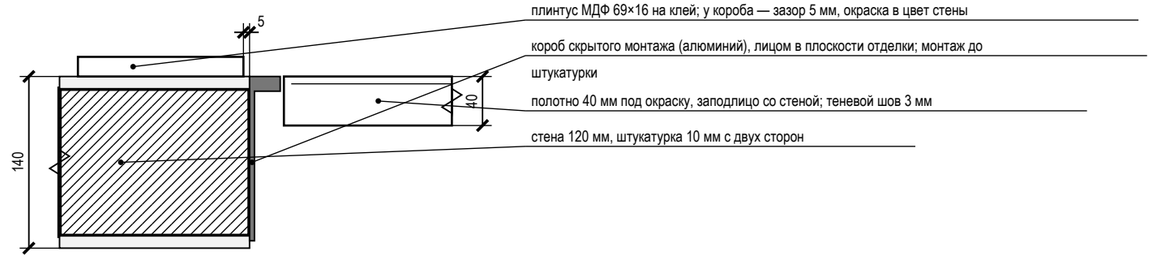


3 Короб стояков К1-1 с люком и звукоизоляцией (М 1:20)

Применение: пом. 6

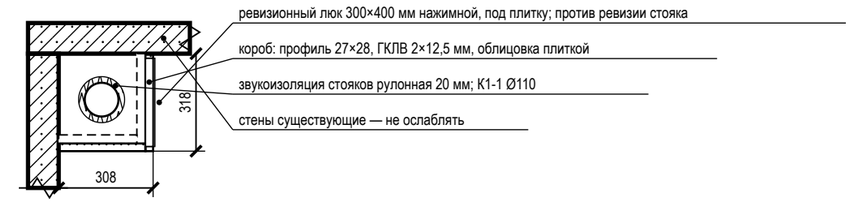


4 Гидроизоляция санузла: заход на стены 200 мм, примыкание ванны (М 1:20)

Применение: пом. 6, 7

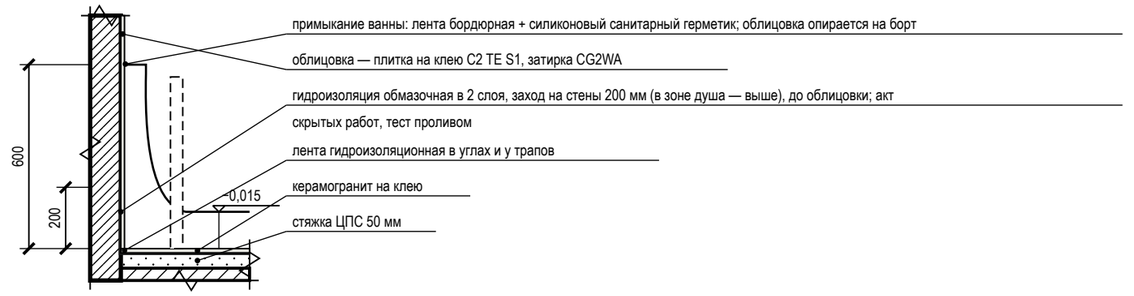

5 Плинтус МДФ 69×16 мм у окрашенной стены (М 1:10)

Применение: пом. 1, 2, 3, 4, 5, 8, 9

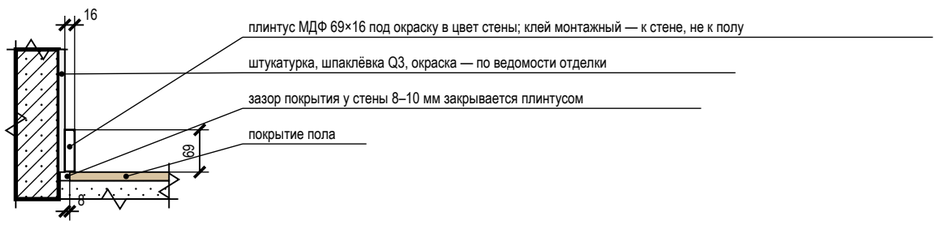

Условные обозначения

- железобетон (плита, стены)
- кладка, перегородка
- стяжка, раствор
- гипсокартон ГКЛВ
- звукоизоляция, эластичный заполнитель
- плитка, керамогранит на клею
- инженерная доска (покрытие пола)
- металлический профиль (порог, Т-профиль, короб двери)
- гидроизоляция (обмазочная, лента)

Примечания

1. Узлы — типовые решения проекта для мест, отмеченных выносками на листе схемы расположения развёрток и узлов; размеры — в мм, отметки — в м от ±0,000.
2. Узлы с гидроизоляцией, закладными и коробами скрытого монтажа принимаются по актам скрытых работ до закрытия отделкой; гидроизоляция — после теста проливом (24 ч).
3. Марки изделий (порог, Т-профиль, короб скрытой двери, люк) — по спецификациям; замена — на аналог с теми же габаритами по согласованию с автором проекта.

					Проект: Квартира 65 м²
	Лист	№ док.	Подпись	Дата	
Дизайнер	Кырлан А.С.			21.10.26	Узлы
					Стадия: П; Лист: С3; Листов: 80

выпуск 09.10.2026 № da691793fd · стр. 80 из 80