LINEA

РАБОЧАЯ ДОКУМЕНТАЦИЯ

Квартира 56 м²

джапанди

ЖК «Северный парк», Москва

Шифр комплекта ГД-2026-011-АИ

Стадия РП

Дата выпуска 19.10.2026

ПРЕДВАРИТЕЛЬНО · не для производства работ
открыто пунктов: 10 (реестр — л. 5)

ДИЗАЙНЕР

Кырлан Александр Сергеевич

выпуск 19.10.2026 № 1c3e34763b · стр. 1 из 117



Содержание

ПРЕДВАРИТЕЛЬНО · не для производства работ · открыто пунктов: 10 (реестр — л. 5)

03 Общие данные 12 л.

15 Архитектурные решения 3 л.

19 Планировочное решение 5 л.

25 Электрооборудование 8 л.

34 Отопление и вентиляция 2 л.

37 Водоснабжение и канализация 5 л.

43 Потолки и ГКЛ-конструкции 7 л.

51 Полы и отделка 6 л.

58 Декор и текстиль 12 л.

71 Развёртки и узлы 15 л.

87 Смета 8 л.

96 Визуализации 21 л.

ДИЗАЙН-ПРОЕКТ ИНТЕРЬЕРА

Квартира 56 м²

джапанди

56,37 м²

тишина · заземлённость · медленная жизнь · тёплый минимализм · ваби-саби · hygge

Джапанди по брифу: стены S 0804-Y30R, потолок Damask F485, серо-зелёный Sea Smoke и дуб под маслом, акценты олива Bancha и тёмный орех; без глянца (К-6).

ПАЛИТРА 60 / 30 / 10

NCS S 0804-Y30R	F485	Little Greene No. 105	X447	V484
60 %	60 %	60 %	30 %	30 %



Визуализация 1 · Вид сверху (3D): планировка с мебелью, текстилем и декором

ОБЪЕКТ	ОБЩАЯ ПЛОЩАДЬ	ПОМЕЩЕНИЙ
Квартира 56 м²	56,37 м²	5, из них жилых 3
СТИЛЬ	**СТАДИЯ**	**ШИФР**
Джапанди	Рабочий проект · предварительно	ГД-2026-011-АИ

АВТОР ПРОЕКТА

Кырлан Александр Сергеевич

Октябрь 2026

Изм.	Кол.уч	Лист	№ док.	Подп.	Дата
Разраб.		Кырлан А.С.			21.10.26
Пров.					
ГИП					
Н. контр.					
Утв.					

ГД-2026-011-АИ

Квартира 56 м²

ЖК «Северный парк», Москва

Дизайн-проект интерьера

Стадия	Лист	Листов
РП	1	83

Титульный лист

М б/м

Кырлан Александр Сергеевич

выпуск 19.10.2026 № 1c3e34763b · стр. 3 из 117

Общие данные

Комплект ГД-2026-011-АИ · Квартира 56 м² · джапанди

ПРЕДВАРИТЕЛЬНО · не для производства работ · открыто пунктов: 10 (реестр — л. 5)

Допущения и предложения на листе. Знак «**» предложено (согласовать). См. лист открытых вопросов (лист 5).

Ведомость рабочих чертежей основного комплекта ГД-2026-011-АИ

Лист	Наименование	Примечание
1	Титульный лист	
2	Общие данные	
3	Общие данные	
4	Общие данные	
5	Открытые вопросы, принятые допущения и конфликты	
6	Задание на контрольный обмер и обследование. Лист 1 из 4	
7	Задание на контрольный обмер и обследование. Лист 2 из 4	
8	Задание на контрольный обмер и обследование. Лист 3 из 4	
9	Задание на контрольный обмер и обследование. Лист 4 из 4	
10	График закупок и работ. Лист 1 из 3	
11	График закупок и работ. Лист 2 из 3	
12	График закупок и работ. Лист 3 из 3	
13	Обмерный план	
14	План демонтажа и монтажа перегородок	
15	План дверей и ведомость заполнения проёмов	
16	Концепция интерьера	
17	План расстановки мебели	
18	Спецификация мебели и оборудования	
19	Спецификация мебели и оборудования (продолжение)	
20	Спецификация мебели и оборудования (продолжение)	
21	План розеток и электровыводов	
22	План освещения	
23	План выключателей и схема включения	
24	Ведомость электроточек и изделий	
25	Ведомость электроточек и изделий (продолжение)	
26	Однолинейная схема щита	
27	План принципиальных трасс	
28	План слаботочных сетей	
29	План вентиляции	
30	План отопления	

Ведомость рабочих чертежей основного комплекта ГД-2026-011-АИ (продолжение)

Лист	Наименование	Примечание
31	План выводов сантехники	
32	Схема разводки водопровода и канализации	
33	Спецификация сантехнического оборудования	
34	Спецификация светильников и сценарии освещения	
35	Схема каркаса перегородки П-2**	
36	План потолков	
37	Разрезы и узлы потолков	
38	Разрезы и узлы потолков (продолжение)	
39	Разрезы и узлы потолков (продолжение)	
40	Раскладка плитки. Планы полов	
41	Раскладка плитки. Прихожая. Фартук кухни	
42	Раскладка плитки. Санузел. Развёртки стен	
43	План полов	
44	Ведомость отделки помещений	
45	Колерная карта	
46	Спецификация отделочных материалов	
47	Концепция декора и визуализации	
48	План текстиля и декора	
49	Шторы и карнизы	
50	Ведомость текстиля	
51	Ведомость декора. Схемы развески	
52	Встроенная мебель. Схема расположения	
53	Шкаф распашной Сп4	

Общие указания — лист 4: ±0,000 — чистый пол; несущие конструкции и сети дома — по отдельному проекту; скрытые работы — по актам. Открытые вопросы и допущения — лист 5.

Изм.	Кол.уч	Лист	№ док.	Подп.	Дата
Разраб.		Кырлан А.С.			21.10.26
Пров.					
ГИП					
Н. контр.					
Утв.					

ГД-2026-011-АИ

Квартира 56 м²

ЖК «Северный парк», Москва

Дизайн-проект интерьера

Стадия	Лист	Листов
РП	2	83

Общие данные

М б/м

Кырлан Александр Сергеевич

выпуск 19.10.2026 № 1c3e34763b · стр. 4 из 117

Общие данные

Комплект ГД-2026-011-АИ · лист 2 общих данных (продолжение)

Ведомость рабочих чертежей основного комплекта ГД-2026-011-АИ (продолжение)

Лист	Наименование	Примечание
54	Шкаф распашной Дт2	
55	Шкаф-купе Пр1	
56	Система хранения Пр3	
57	Кухня (пом. 1). Развёртка гарнитура	
58	Кухня (пом. 1). Монтажная схема	
59	Шкафы. Монтажная схема	
60	Ведомости изделий, техники и фурнитуры	
61	Реестр марок отделки и позиций альбома	
62	Схема расположения развёрток и узлов	
63	Развёртка стены Г. Гостиная-кухня (пом. 1), кухонный фронт	
64	Развёртки стен А, Б. Гостиная-кухня (пом. 1)	
65	Развёртка стены В. Гостиная-кухня (пом. 1)	
66	Развёртки стен А, Б. Спальня (пом. 2)	
67	Развёртки стен В, Г. Спальня (пом. 2)	
68	Развёртки стен А, Б. Детская (пом. 3)	
69	Развёртки стен В, Г. Детская (пом. 3)	
70	Развёртка стены А. Санузел (пом. 4)	
71	Развёртки стен Б, В. Санузел (пом. 4)	
72	Развёртка стены Г. Санузел (пом. 4)	
73	Развёртки стен А, Б. Прихожая (пом. 5)	
74	Развёртки стен В, Г. Прихожая (пом. 5)	
75	Узлы	
76	Ведомость объёмов работ	
77	Ведомость объёмов работ (продолжение)	
78	Ведомость объёмов работ (окончание)	
79	Спецификация материалов	
80	Спецификация материалов (продолжение)	
81	Спецификация материалов (окончание)	
82	Смета ориентировочная Допущения и предложения на листе. См. лист открытых вопросов (лист 5).	
83	Смета ориентировочная (окончание)	

Ведомость ссылочных и прилагаемых документов

Обозначение	Наименование	Примечание
	Ссылочные документы	
ГОСТ 21.201-2011	СПДС. Условные графические изображения элементов зданий, сооружений и конструкций	
ГОСТ 21.205-2016	СПДС. Условные обозначения элементов санитарно-технических систем	
ГОСТ 21.210-2014	СПДС. Изображения условные графические электрооборудования и проводок на планах	
ГОСТ 2.306-68	ЕСКД. Обозначения графические материалов и правила их нанесения на чертежах	
	Прилагаемые документы	
ГД-2026-011-АИ.В1	Визуализация. Вид сверху (3D): планировка с мебелью, текстилем и декором	альбом визуализаций
ГД-2026-011-АИ.В2	Визуализация. Визуализация «room-bath-wA»	
ГД-2026-011-АИ.В3	Визуализация. Визуализация «room-bath-wB»	
ГД-2026-011-АИ.В4	Визуализация. Визуализация «room-bath-wC»	
ГД-2026-011-АИ.В5	Визуализация. Визуализация «room-bath-wD»	
ГД-2026-011-АИ.В6	Визуализация. Визуализация «room-bedroom-wA»	
ГД-2026-011-АИ.В7	Визуализация. Визуализация «room-bedroom-wB»	
ГД-2026-011-АИ.В8	Визуализация. Визуализация «room-bedroom-wC»	
ГД-2026-011-АИ.В9	Визуализация. Визуализация «room-bedroom-wD»	
ГД-2026-011-АИ.В10	Визуализация. Визуализация «room-hall-wA»	
ГД-2026-011-АИ.В11	Визуализация. Визуализация «room-hall-wB»	
ГД-2026-011-АИ.В12	Визуализация. Визуализация «room-hall-wC»	
ГД-2026-011-АИ.В13	Визуализация. Визуализация «room-hall-wD»	
ГД-2026-011-АИ.В14	Визуализация. Визуализация «room-kids-wA»	
ГД-2026-011-АИ.В15	Визуализация. Визуализация «room-kids-wB»	
ГД-2026-011-АИ.В16	Визуализация. Визуализация «room-kids-wC»	

Общие указания — лист 4: ±0,000 — чистый пол; несущие конструкции и сети дома — по отдельному проекту; скрытые работы — по актам. Открытые вопросы и допущения — лист 5.

Изм.	Кол.уч	Лист	№ док.	Подп.	Дата
Разраб.		Кырлан А.С.			21.10.26
Пров.					
ГИП					
Н. контр.					
Утв.					

ГД-2026-011-АИ

Квартира 56 м²

ЖК «Северный парк», Москва

Дизайн-проект интерьера

Стадия	Лист	Листов
РП	3	83

Общие данные

М б/м

Кырлан Александр Сергеевич

выпуск 19.10.2026 № 1c3e34763b · стр. 5 из 117

Общие данные

Комплект ГД-2026-011-АИ · лист 3 общих данных (продолжение)

Ведомость ссылочных и прилагаемых документов (продолжение)

Обозначение	Наименование	Примечание
ГД-2026-011-АИ.В17	Визуализация. Визуализация «room-kids-wD»	
ГД-2026-011-АИ.В18	Визуализация. Визуализация «room-living-wA»	
ГД-2026-011-АИ.В19	Визуализация. Визуализация «room-living-wB»	
ГД-2026-011-АИ.В20	Визуализация. Визуализация «room-living-wC»	
ГД-2026-011-АИ.В21	Визуализация. Визуализация «room-living-wD»	

Состав дизайн-проекта

Раздел	Состав	Листы
Обложка	Дизайн-проект интерьера; Квартира 56 м²; автор проекта — Кырлан Александр Сергеевич	1 с.
Концепция	Стиль Джапанди: концепция интерьера, палитра и материалы (колерная карта — лист 45)	л. 16
Визуализации	21 изобр.: Вид сверху (3D): планировка с мебелью, текстилем и декором; Визуализация «room-bath-wA»; Визуализация «room-bath-wB»; Визуализация «room-bath-wC»; Визуализация «room-bath-wD»; Визуализация «room-bedroom-wA»; Визуализация «room-bedroom-wB»; Визуализация «room-bedroom-wC»; Визуализация «room-bedroom-wD»; Визуализация «room-hall-wA»; Визуализация «room-hall-wB»; Визуализация «room-hall-wC»; Визуализация «room-hall-wD»; Визуализация «room-kids-wA»; Визуализация «room-kids-wB»; Визуализация «room-kids-wC»; Визуализация «room-kids-wD»; Визуализация «room-living-wA»; Визуализация «room-living-wB»; Визуализация «room-living-wC»; Визуализация «room-living-wD»	В1–В21
Рабочие чертежи	планы, развёртки, узлы (развёртки и узлы — листы 62, 64, 66–69, 71, 73–75)	л. 1–83
Спецификации и ведомости	оборудование, изделия, отделка, электроточки	л. 15, 18–20, 24, 25, 33, 34, 44–46, 50, 51, 76–81

Условные обозначения

- контрольный отрезок 1000 мм натуры: по нему проверяют печать 1:1
- отметка уровня, м: ±0,000 — чистый пол жилых помещений
- А — марка развёртки: буква стены, стрелка — взгляд
- О1 — марка отделки по реестру отделки альбома
- выноска узла: над полкой — узел, под полкой — лист

Общие указания

1. Рабочие чертежи интерьера разработаны на основании задания на проектирование и обмерного плана (лист 13). Объект: Квартира 56 м², ЖК «Северный парк», Москва; автор проекта — Кырлан Александр Сергеевич; общая площадь 56,37 м², жилая 42,98 м², помещений 5.
2. Рабочие чертежи выполнены в соответствии с заданием на проектирование и нормативными документами, перечисленными в п. 4.
3. Открытые вопросы, принятые допущения и конфликты между разделами, не снятые к выпуску комплекта, сведены в таблицы на листе 5. До ответа по пункту таблицы показанное на указанном там листе — допущение, а не утверждённое решение: комплект по этим листам предварительный.
4. Нормативные документы, на которые есть ссылки в листах комплекта: ГОСТ Р 21.101-2026; ГОСТ 21.501-2018; ГОСТ 2.302-68; ГОСТ 2.303-68; ГОСТ 2.304-81; ГОСТ 2.307-2011; СП 54.13330.2022; СП 71.13330.2017; СП 73.13330.2016; ПУЭ (7-е изд.), гл. 1.8, 7.1; ГОСТ Р 50571.7.701-2024; СанПиН 1.2.3685-21; ГОСТ 2.702; ГОСТ 2.755; ГОСТ 21.110-2013; ГОСТ 21.601; ГОСТ 13996-2019; ГОСТ 23166-2021; ГОСТ 31565-2012; ГОСТ 31975; ГОСТ 32414-2013; ГОСТ 32415-2013; ГОСТ 32614-2012; ГОСТ Р 56387-2018; СП 15.13330; СП 29.13330.2011; СП 30.13330.2020; СП 51.13330.2011; СП 52.13330.2016; СП 131.13330. Документы из ведомости ссылочных документов здесь не повторяются.
5. За отметку ±0,000 принят уровень чистого пола жилых помещений квартиры (относительная отметка; абсолютная — по проекту дома). Отметка чистого пола мокрых помещений — −0,015. Размеры — в миллиметрах, отметки — в метрах, площади — в м²; высоты установки Н от чистого пола своего помещения до оси изделия.
6. Несущие конструкции, общедомовые стояки, вентиляционные каналы и инженерные сети дома настоящим комплектом не изменяются. Работы, затрагивающие их (проём или штраба в несущей стене, перенос стояка, врезка в вентканал, расширение мокрой зоны), выполняются только по отдельному проекту, к которому прилагается техническое заключение о допустимости и безопасности работ, выданное автором проекта дома или организацией с допуском на обследование, и который согласован в установленном порядке (Жилищный кодекс РФ, ст. 25–29).
7. Трассы инженерных сетей на листах — принципиальные. Расчёты электрических нагрузок и токов КЗ, гидравлики, воздухообмена, освещённости и нагрузок на перекрытие выполняются в проектах ЭОМ, ВК, ОВ и КР организацией с допуском СРО; фактические трассы до закрытия отделкой фиксируются исполнительными схемами.
8. Стиль интерьера — Джапанди. Палитра проекта: основной 60 % — NCS S 0804-Y30R «S 0804-Y30R», Tikkurila F485 «Damask», Little Greene No. 105 «Slaked Lime»; дополнительный 30 % — Tikkurila X447 «Sea Smoke», Tikkurila V484 «Driftwood», NCS S 2005-Y30R «S 2005-Y30R»; акцент 10 % — Farrow & Ball No. 298 «Bancha», NCS S 5010-G70Y «S 5010-G70Y», NCS S 7005-Y20R «S 7005-Y20R». Коды цвета — по веерам производителей; цвет утверждается по выкрасу на объекте при освещении проекта.
9. Площади поверхностей — по чистым граням стен до отделки: стены = периметр × высоту от чистого пола помещения до низа потолка минус проёмы (облицовка плиткой — до верха облицовки); плинтус = периметр минус дверные проёмы; пол и потолок — по площади помещения. Количество плиток — по раскладке. Способ один для всех листов комплекта (ведомость отделки, колерная карта, раскладка плитки, развёртки).
10. Марки: стены помещения на всех листах — А (верхняя по плану), Б (правая), В (нижняя), Г (левая); марка отделки О — одна на весь альбом; реестр марок отделки (с позициями колерной карты той же отделки) и марки позиций по видам — на листе 61.
11. Развёртки стен выполнены по всем помещениям для стен с электроточками, мебелью, декором и отделкой: санузлы и кухонный фронт — в М 1:25, остальные стены — в М 1:40; расположение развёрток и узлов — на листе 62, узлы — на листе 75.
12. Перечень скрытых работ, на которые составляются акты освидетельствования (форма по приказу Минстроя России № 344/пр): гидроизоляция пола и стен мокрых помещений (с тестом проливом); стяжка пола (толщина, прочность, влажность основания); скрытая электропроводка (за потолком и в штробах стен; условия штробления — в следующем пункте); трубопроводы водоснабжения и канализации до закрытия (опрессовка, уклоны); закладные и усиления под подвесные приборы, мебель и тяжёлый декор, рамы инсталляций; короба дверей скрытого монтажа до штукатурки; каркасы ГКЛ потолков, коробов и перегородок до обшивки.
13. Скрытая электропроводка: за потолком и в штробах стен. Штробы в стенах выполняются только после технического заключения о несущих конструкциях; до заключения несущие стены не определены, и все стены считаются несущими; объём штроб — в ведомости объёмов работ, строка «Штробы в стенах» (вертикальные спуски; объём не меньше фактического, горизонтальные трассы — по исполнительной схеме).
14. Критерии приёмки: допуски отделочных покрытий — по СП 71.13330.2017; испытания систем водоснабжения и канализации — по СП 73.13330.2016 до закрытия трасс; приёмо-сдаточные испытания электроустановки — по ПУЭ, гл. 1.8, с протоколом электролаборатории.
15. Осознанные отступления от ГОСТ Р 21.101-2026, принятые в комплекте: номер листа и число листов («Листов») указаны на каждом листе; на масштабных листах в основной надписи указан фактический масштаб и дан контрольный отрезок 1000 мм; развёртки стен выполнены в М 1:25 и 1:40 (ГОСТ 21.507-81 — 1:50…1:500) ради читаемости привязок; размерные числа и марки элементов (Д-1, ОК-1, О6) — кеглем 2,5 мм, номера помещений — в кружке Ø 8 мм (канон — 3,5 мм и Ø 12 мм): так насыщенные листы А3 читаются без наложений надписей.
16. Графы «Пров.», «Н. контр.», «Утв.» основной надписи заполняются при согласовании комплекта с заказчиком; до согласования комплект подписывает автор проекта (графа «Разраб.»).

Допущения и предложения на листе

Основа листа: размеры помещений и положение проёмов введены заказчиком в брифе, на объекте не замерены (К-1); высота потолка 2700 мм — по брифу заказчика, не замерена (К-2); толщины стен приняты по брифу: наружные 200 мм, внутренние 150 мм — не обмерены (К-1); тип дома монолитный, перекрытие 200 мм — по брифу заказчика, документов нет (К-3); планировка (стены, проёмы, объединение кухни и гостиной, расширение санузла) — по брифу без обмера и плана БТИ (К-7); разрешённая мощность 10 кВт принята, ТУ не переданы (К-8); вентканалы приняты, в брифе не заданы (К-9); подрайон климата не задан — принят не северный (жилые от 2,5 м) (К-10).
См. лист открытых вопросов (лист 5, записи К-1–К-3, К-7–К-10).

Изм.	Кол.уч	Лист	№ док.	Подп.	Дата			
Разраб.		Кырлан А.С.			21.10.26	ГД-2026-011-АИ		
Пров.						Квартира 56 м² ЖК «Северный парк», Москва		
ГИП						Дизайн-проект интерьера	Стадия: РП	Лист: 4 / Листов: 83
Н. контр.						**Общие данные** М б/м	**Кырлан Александр Сергеевич**	
Утв.								

выпуск 19.10.2026 № 1c3e34763b · стр. 6 из 117

Открытые вопросы, принятые допущения и конфликты

Сводка по реестрам координации (стартовое совещание 19.10.2026)

Комплект предварительный по пунктам этих таблиц. Пока по пункту нет ответа или решения, показанное на указанном листе — допущение проектировщика, а не утверждённое решение.
Сводка: открытых вопросов — 10 (из них ждут факта объекта — 8: контрольного обмера, обследования или документа).
Пункты, ответ на которые лежит на объекте, а не за столом проектировщика (графа «Вид», строка «Ждёт»), собраны на листе «Задание на контрольный обмер и обследование» (листы 6–9): что и где замерить, с какой точностью и чем подтвердить. Пункты, ждущие решения человека, на объекте не закрываются.

Открытые вопросы и принятые допущения

№	Формулировка	Вид	Кто решает	Если решения нет	Лист, где это проявляется
К-1	Размеры помещений, толщины стен (наружные 200 мм, перегородки 150 мм) и положение проёмов введены заказчиком в бриф заказчика (site-brief-wizard, 01.08.2026): контрольный обмер на объекте не выполнялся, обмерного плана и плана БТИ в материалах нет; площадь по брифу 56 м², сумма помещений по чистым размерам брифа 56.37 м². От этого зависят все размеры альбома, площади, заказ материалов и изделий. Выполнить контрольный обмер.	Непонятно Ждёт: обмера	Архитектор-планировщик	все размеры альбома остаются по брифу заказчика и не считаются замеренными; заказ изделий по ним не ведётся	л. 13 — Обмерный план л. 15 — План дверей и ведомость заполнения проёмов
К-2	Высота потолка 2700 мм указана заказчиком в брифе, на объекте не замерена. От неё зависят вертикальные размеры альбома (развёртки, шкафы, перегородки, объёмы работ). Замерить высоту на объекте.	Непонятно Ждёт: обмера	Архитектор-планировщик	вертикальные размеры альбома остаются по брифу и не считаются замеренными	л. 13 — Обмерный план
К-3	Тип дома (монолитный) и толщина перекрытия 200 мм указаны заказчиком в брифе; проект дома, план БТИ и техническое заключение о несущих конструкциях не переданы. Несущие стены и допустимость демонтажа определяются только по этим документам или по обследованию.	Отсутствует Ждёт: документа, обследования	Архитектор-планировщик	все существующие стены считаются несущими; демонтаж и штробление в них не выполняются до технического заключения	л. 13 — Обмерный план л. 14 — План демонтажа и монтажа перегородок
К-4	Положение и диаметры стояков (канализации, холодной воды) указаны заказчиком в брифе, не замерены; врезки, краны и счётчики не описаны. От стояков зависят трассы водопровода и канализации, привязки выводов и уклоны. Замерить на объекте.	Непонятно Ждёт: обмера	Инженер ВК (вода, канализация)	трассы и привязки выводов остаются по положению стояков из брифа и не считаются замеренными	л. 31 — План выводов сантехники л. 32 — Схема разводки водопровода и канализации
К-5	Новые перегородки заданы заказчиком в брифе положением, материалом и толщиной; конструкция (система, число слоёв, каркас, звукоизоляция, Rw) выбрана исполнителем по каталогам. Утвердить конструкцию перегородок или задать другую.	Спорно Ждёт: решения	Архитектор-планировщик	конструкция перегородок остаётся по решению исполнителя со знаком «предложено»	л. 14 — План демонтажа и монтажа перегородок
К-6	Цвета названы заказчиком в брифе словами (тёплый белый, натуральное дерево, серо-зелёный). Исполнитель перевёл их в коды по веерам стиля джапанди: стены NCS S 0804-Y30R, потолки Tikkurila F485 Damask, второй план Tikkurila X447 Sea Smoke и V484 Driftwood, акценты Farrow & Ball No. 298 Bancha и NCS S 5010-G70Y (по комнатам). Выкрасы на объекте не делались. Утвердить коды по выкрасам. Матовость: в брифе в «не нравится» — «Глянец, холодный белый», поэтому стены матовые (в кухне-гостиной и прихожей — матовая моющаяся краска вместо полуматовой, класс мойки — по ведомости отделки); подтвердить вместе с кодами.	Спорно Ждёт: решения	Колорист-комплектатор	коды — предложение исполнителя; краску не закупать до выкрасов	л. 45 — Колерная карта
К-7	Планировка принята по брифу заказчика: положение существующих стен и проёмов, объединение кухни с гостиной (демонтаж С-1), расширение санузла (демонтаж С-2, перегородка П-1) введены в мастер брифа без обмерного плана и плана БТИ. Расстановка мебели и кухни, рабочее место в спальне, антресоль в прихожей — предложение исполнителя по этой планировке. Нужны план БТИ и контрольный обмер; до них планировочное решение — предварительное.	Непонятно Ждёт: документа	Архитектор-планировщик	расстановка остаётся предложением; мебель на заказ (кухня, шкафы) не заказывать	л. 13 — Обмерный план л. 14 — План демонтажа и монтажа перегородок л. 17 — План расстановки мебели
К-8	Разрешённая мощность квартиры по ТУ в брифе не указана; принята 10 кВт (квартира с электроплитой, монолитный дом). Передать ТУ или справку УК.	Отсутствует Ждёт: документа	Инженер-электрик	щит и группы рассчитаны на 10 кВт; при меньших ТУ пересчёт групп варочной панели и духового шкафа	л. 26 — Однолинейная схема щита
К-9	Вентканалы в брифе не показаны: принято два канала — ВК-1 в санузле у стояков (стена А) и ВК-2 у стены В бывшей кухни. От них зависят вытяжка санузла, вытяжка над плитой (до обмера — рециркуляция) и короба потолка. Замерить положение и сечение на объекте.	Отсутствует Ждёт: обмера	Инженер ОВ	вытяжка кухни — рециркуляционная; вентилятор санузла по месту ВК-1 после обмера	л. 29 — План вентиляции л. 31 — План выводов сантехники
К-10	Климатический подрайон (СП 131.13330) не задан: принят не северный — жилые комнаты и кухня под потолком от 2,5 м (СП 54, п. 5.12); в IA, IБ, IГ, IД, IVA — от 2,7 м.	Отсутствует Ждёт: документа	Архитектор-планировщик	отметки потолков жилых — по 2,5 м; при северном подрайоне уровни ниже 2,7 м пересчитать до заказа каркаса	л. 36 — План потолков

Примечания

1. Номера листов — по ведомости рабочих чертежей комплекта (лист «Общие данные»).
2. Графа «Если решения нет» показывает состояние решения на листах; влияние на сроки и стоимость по пунктам не оценивалось.
3. Пункт, по которому принято решение, при следующем выпуске комплекта из таблиц исключается.

Изм.	Кол.уч	Лист	№ док.	Подп.	Дата	ГД-2026-011-АИ			
						Квартира 56 м² ЖК «Северный парк», Москва			
Разраб.		Кырлан А.С.			21.10.26	Дизайн-проект интерьера	Стадия	Лист	Листов
Пров.							РП	5	83
ГИП									
Н. контр.						**Открытые вопросы, принятые допущения и конфликты** М б/м	**Кырлан Александр Сергеевич**		
Утв.									

Задание на контрольный обмер и обследование. Лист 1 из 4

ПРЕДВАРИТЕЛЬНО · не для производства работ · открыто пунктов: 10 (реестр — л. 5)

Что замерить, вскрыть и получить до заказа материалов и изделий

Задание собрано из открытых вопросов, ответ на которые лежит на объекте или в документах, а не за столом проектировщика. Пока факт не получен, размер, материал или положение на листах — допущение (знак «*»), а не замер.
Сводка: на объекте — 16 (до демонтажа — 14; после демонтажа — 2); документом и при закупке — 4; из допущений в данных и на листах — 16, из них без вопроса в реестре — 4. Закрываются вопросы: К-1–К-4, К-7–К-10 (8). Вопросы, ждущие решения человека, задание не закрывает — они решаются по реестру открытых вопросов.

Условия проведения

Порядок работ	Приёмы и точность	Кто присутствует	Если факт не совпал с проектом
1. До демонтажа — существующее состояние: контур, диагонали, высоты, проёмы, оси стояков, ниши и конструкции, которые видны. 2. После демонтажа, до черновых работ — то, что закрывали отделка и короба: основание стен, фактические толщины, углы, узлы. 3. Документы и данные закупки — не на объекте: к сроку из последней таблицы, от них зависят привязки и заказ. Что заказывается по размеру из задания, до закрытия пункта не заказывают: сроки изготовления — по графику закупок прораба.	Обход по часовой стрелке от входа: стены, проёмы, потолок, коммуникации (стояки, щиток, вентканалы), особенности (ниши, короба, выступы). Размеры записывают в мм; сумма участков равна общему размеру, при цепочке длиннее трёх участков ставят проверочный (общий) размер. Диагонали каждого помещения; если две диагонали различаются на 5 мм и больше, разницу подписывают на плане. Потолок — в нескольких точках: центр, углы, у проёмов. Проём — ширина, высота, глубина откоса, привязка к ближайшим углам, высота подоконника. Допустимая погрешность прибора — 2–3 мм на метр; размеры округляют кратно 5 мм; два контрольных промера одного размера не должны расходиться более чем на 2 %. Допуск по пункту — в графе «Точность». План БТИ обмер не заменяет.	Прораб (отвечает за проведение) — назначает день и порядок обхода, открывает объект и освобождает помещения, ведёт это задание и реестр изменений. Архитектор — выполняет обмер, составляет акт контрольного обмера и подписывает результаты по размерам и конструкциям. Владельцы вопросов присутствуют при пунктах своего раздела или принимают результат до заказа: Инженер ВК (вода, канализация) — К-4; Инженер-электрик — К-8; позиции О-1; Инженер ОВ — К-9; позиции О-2; Отделочник — позиции О-15, О-16. Технадзор — при вскрытиях и обследованиях: фото с рулеткой до закрытия. Заказчик или его представитель — передаёт документы (план БТИ, проект дома, технические условия, паспорта), подписывает акт. Проектных решений на обмере не принимают: обмер даёт факт, решения — по реестру открытых вопросов (лист 5).	1. В пределах допуска пункта — принимается измеренное значение, лист перевыпускается, знак «*» снимается. 2. Больше допуска или контрольные промеры расходятся более чем на 2 % — промер повторяют; не подтвердилось — запись в реестр изменений (дата, лист, было, стало, кто решил, подпись), работы в этом месте не начинают. 3. Затронуты несущая стена, стояк, вентканал или мокрая зона — сразу владельцу раздела и ГИПу (главному инженеру проекта); между разделами не больше двух кругов, затем решает ГИП. 4. На объекте устно ничего не согласуется: каждое решение — записью в реестр с подписью.

Этап 1. До демонтажа

№	Где	Способ	Что сделать	Кто выполняет	Точность	Что пересчитается в альбоме	Чем подтверждается	Закрывает вопросы реестра
О-1	Вход в квартиру или лестничная клетка; место щита на плане	Обмер	Существующий щиток и счётчик электроэнергии: место и габарит ниши, состояние ввода, марка и сечение вводного кабеля, наличие вводного автомата и УЗО, пломбы.	Архитектор	±5 мм	Ниша и место щита на листах; вводной кабель и аппараты на однолинейной схеме; расстояния до первых групп. Листы: л. 26 — Однолинейная схема щита	акт контрольного обмера; фото с рулеткой и привязкой к стене или углу	Вопроса в реестре нет: Альбом принимает щит и ввод без осмотра. Результат принимает: Инженер-электрик
О-2	Гостиная-кухня (пом. 1), Спальня (пом. 2), Детская (пом. 3); у окон	Обмер	Положение стояков отопления (подающий и обратный) от граней стен, диаметры, наличие запорной арматуры; существующие радиаторы: число секций, межосевое расстояние, подводки. В данных стояков отопления нет — лист отопления выводит их условно у откоса окна, радиаторы — «принципиально, по расчёту».	Архитектор	±5 мм	План отопления: места стояков и подводок, привязки радиаторов; подбор радиаторов по теплотехническому расчёту; радиаторы и узлы подключения в ВОР и спецификации. Листы: л. 30 — План отопления	акт контрольного обмера; фото с рулеткой и привязкой к стене или углу	Вопроса в реестре нет: Альбом принимает положение стояков и радиаторов отопления без обмера. Результат принимает: Инженер ОВ
О-3	Вся квартира, все помещения; обход по часовой стрелке от входа	Обмер	Контрольный обмер всех помещений: чистые размеры, диагонали, толщины стен (по брифу 200 мм наружные и 150 мм внутренние), положение и размеры существующих проёмов дверей и окон, подоконники, высота проёмов.	Архитектор	±5 мм; диагонали — разница от 5 мм подписывается	Чистые размеры и площади помещений, толщины стен, положение проёмов; размеры, по которым заказываются материалы и изделия. Листы: л. 13 — Обмерный план л. 15 — План дверей и ведомость заполнения проёмов	акт контрольного обмера	К-1 Результат принимает: Архитектор
О-4	Все помещения квартиры	Обмер	Высота потолка в каждом помещении в нескольких точках: центр, углы, у проёмов. По брифу 2700 мм.	Архитектор	±5 мм	Вертикальные размеры альбома: развёртки, перегородки, шкафы, объёмы работ. Листы: л. 13 — Обмерный план	акт контрольного обмера	К-2 Результат принимает: Архитектор

Допущения и предложения на листе
Основа листа: размеры помещений и положение проёмов введены заказчиком в брифе, на объекте не замерены (К-1); высота потолка 2700 мм — по брифу заказчика, не замерена (К-2); толщины стен приняты по брифу: наружные 200 мм, внутренние 150 мм — не обмерены (К-1); тип дома монолитный, перекрытие 200 мм — по брифу заказчика, документов нет (К-3); планировка (стены, проёмы, объединение кухни и гостиной, расширение санузла) — по брифу без обмера и плана БТИ (К-7); разрешённая мощность 10 кВт принята, ТУ не переданы (К-8); вентканалы приняты, в брифе не заданы (К-9); подрайон климата не задан — принят не северный (жилые от 2,5 м) (К-10).
См. лист открытых вопросов (лист 5, записи К-1–К-3, К-7–К-10).

Изм.	Кол.уч	Лист	№ док.	Подп.	Дата
Разраб.		Кырлан А.С.			21.10.26
Пров.					
ГИП					
Н. контр.					
Утв.					

ГД-2026-011-АИ

Квартира 56 м²

ЖК «Северный парк», Москва

Дизайн-проект интерьера

Стадия	Лист	Листов
РП	6	83

Задание на контрольный обмер и обследование.
Лист 1 из 4
М б/м

Кырлан Александр Сергеевич

выпуск 19.10.2026 № 1c3e34763b · стр. 8 из 117

Задание на контрольный обмер и обследование. Лист 2 из 4

Что замерить, вскрыть и получить до заказа материалов и изделий

ПРЕДВАРИТЕЛЬНО · не для производства работ · открыто пунктов: 10 (реестр — л. 5)

Этап 1. До демонтажа (продолжение)

№	Где	Способ	Что сделать	Кто выполняет	Точность	Что пересчитается в альбоме	Чем подтверждается	Закрывает вопросы реестра
О-5	Стены по плану демонтажа; перекрытие в зоне новых перегородок	Обследование	Обследование конструкций: материал и несущая способность стен, подлежащих демонтажу, конструкция перекрытия.	специализированная организация по договору с заказчиком	по методике организации	План демонтажа и монтажа; основания демонтажа (техзаключение). Листы: л. 13 — Обмерный план л. 14 — План демонтажа и монтажа перегородок	техническое заключение	К-3 Результат принимает: Архитектор
О-6	Санузел (пом. 4): Ст К1-1*, Ст В1-1*; наличие стояка ГВС, арматуры и счётчиков — по всей квартире	Обмер	Положение стояков Ст К1-1*, Ст В1-1*: привязка осей от граней стен, диаметры, размеры короба и люков. Стояк горячей воды Т3 в данных не задан, на листах ВК принят рядом с Ст В1-1*: выяснить, есть ли он в доме, и где. Отключающая арматура и счётчики воды на вводах: положение, тип, пломбы управляющей компании. Сверить до разметки выводов.	Архитектор	±5 мм	Привязки выводов воды и канализации на планах выводов и разводки; расстояние розеток до стояка; места люков 300 × 400 мм; трассы Т3 и полотенцесушители (водяной или электрический); узлы ввода в спецификации ВК (краны, фильтры, счётчики). Трассы В1, Т3, К1, привязки выводов сантехники, уклоны канализации, короба стояков. Листы: л. 31 — План выводов сантехники л. 32 — Схема разводки водопровода и канализации	акт контрольного обмера; фото с рулеткой и привязкой к стене или углу	К-4 Результат принимает: Инженер ВК (вода, канализация)
О-7	По месту	Обмер	Подтвердить на объекте принятое: планировка (стены, проёмы, объединение кухни и гостиной, расширение санузла) — по брифу без обмера и плана БТИ	Архитектор	±5 мм	Листы, где используется принятая величина. Листы: л. 2–4 — Общие данные	акт контрольного обмера	К-7 Результат принимает: Архитектор
О-8	По месту	Обмер	Подтвердить на объекте принятое: вентканалы приняты, в брифе не заданы	Архитектор	±5 мм	Листы, где используется принятая величина. Листы: л. 2–4 — Общие данные	акт контрольного обмера	К-9 Результат принимает: Инженер ОВ
О-9	санузел, кухня	Обмер	Положение и сечение вентканалов, тяга.	исполнитель	±10 мм	план вентиляции, потолки, вытяжка кухни Листы: л. 29 — План вентиляции л. 31 — План выводов сантехники	акт контрольного обмера	К-9 Результат принимает: Инженер ОВ
О-10	По месту	Обмер	Подтвердить на объекте принятое: подрайон климата не задан — принят не северный (жилые от 2,5 м)	Архитектор	±5 мм	Листы, где используется принятая величина. Листы: л. 2–4 — Общие данные	акт контрольного обмера	К-10 Результат принимает: Архитектор
О-11	Гостиная-кухня (пом. 1): окно пом. 1, стена А, дверь пом. 1, стена В	Обмер	Окно пом. 1, стена А, дверь пом. 1, стена В: положение (привязки к ближайшим углам), ширина, высота, высота подоконника, глубина откоса. Принято в проекте: окно: положение, ширина, высота и подоконник — по брифу заказчика, не замерены; ограждение 900 мм — предложение исполнителя, проём в существующей стене между пом. 1 и 5: положение и ширина — по брифу заказчика, не замерены.	Архитектор	±5 мм	Проёмы на обмерном плане и в ведомости проёмов; откосы и оконные работы в ВОР; привязки мебели и выводов к проёмам. Листы: л. 13 — Обмерный план л. 15 — План дверей и ведомость заполнения проёмов	акт контрольного обмера; фото с рулеткой и привязкой к стене или углу	К-1 Результат принимает: Архитектор
О-12	Спальня (пом. 2): окно пом. 2, стена А, дверь пом. 2, стена В	Обмер	Окно пом. 2, стена А, дверь пом. 2, стена В: положение (привязки к ближайшим углам), ширина, высота, высота подоконника, глубина откоса. Принято в проекте: окно: положение, ширина, высота и подоконник — по брифу заказчика, не замерены, проём в существующей стене между пом. 2 и 5: положение и ширина — по брифу заказчика, не замерены.	Архитектор	±5 мм	Проёмы на обмерном плане и в ведомости проёмов; откосы и оконные работы в ВОР; привязки мебели и выводов к проёмам. Листы: л. 13 — Обмерный план л. 15 — План дверей и ведомость заполнения проёмов	акт контрольного обмера; фото с рулеткой и привязкой к стене или углу	К-1 Результат принимает: Архитектор

Допущения и предложения на листе

Основа листа: размеры помещений и положение проёмов введены заказчиком в брифе, на объекте не замерены (К-1); высота потолка 2700 мм — по брифу заказчика, не замерена (К-2); толщины стен приняты по брифу: наружные 200 мм, внутренние 150 мм — не обмерены (К-1); тип дома монолитный, перекрытие 200 мм — по брифу заказчика, документов нет (К-3); планировка (стены, проёмы, объединение кухни и гостиной, расширение санузла) — по брифу без обмера и плана БТИ (К-7); разрешённая мощность 10 кВт принята, ТУ не переданы (К-8); вентканалы приняты, в брифе не заданы (К-9); подрайон климата не задан — принят не северный (жилые от 2,5 м) (К-10).

Знак «*» — принято, не замерено и не подтверждено (замерить на объекте): К-4: Ст К1-1 — положение стояка канализации — по брифу заказчика, не замерено; Ст В1-1 — положение стояка холодной воды — по брифу заказчика, не замерено.

См. лист открытых вопросов (лист 5, записи К-1–К-4, К-7–К-10).

Изм.	Кол.уч	Лист	№ док.	Подп.	Дата
Разраб.		Кырлан А.С.			21.10.26
Пров.					
ГИП					
Н. контр.					
Утв.					

ГД-2026-011-АИ

Квартира 56 м²

ЖК «Северный парк», Москва

Дизайн-проект интерьера

Стадия	Лист	Листов
РП	7	83

Задание на контрольный обмер и обследование.
Лист 2 из 4
М б/м

Кырлан Александр Сергеевич

выпуск 19.10.2026 № 1c3e34763b · стр. 9 из 117

Задание на контрольный обмер и обследование. Лист 3 из 4

ПРЕДВАРИТЕЛЬНО · не для производства работ · открыто пунктов: 10 (реестр — л. 5)

Что замерить, вскрыть и получить до заказа материалов и изделий

Этап 1. До демонтажа (продолжение)

№	Где	Способ	Что сделать	Кто выполняет	Точность	Что пересчитается в альбоме	Чем подтверждается	Закрывает вопросы реестра
О-13	Детская (пом. 3): окно пом. 3, стена В	Обмер	Окно пом. 3, стена В: положение (привязки к ближайшим углам), ширина, высота, высота подоконника, глубина откоса. Принято в проекте: окно: положение, ширина, высота и подоконник — по брифу заказчика, не замерены.	Архитектор	±5 мм	Проёмы на обмерном плане и в ведомости проёмов; откосы и оконные работы в ВОР; привязки мебели и выводов к проёмам. Листы: л. 13 — Обмерный план л. 15 — План дверей и ведомость заполнения проёмов	акт контрольного обмера; фото с рулеткой и привязкой к стене или углу	К-1 Результат принимает: Архитектор
О-14	Прихожая (пом. 5): дверь пом. 5, стена В	Обмер	Дверь пом. 5, стена В: положение (привязки к ближайшим углам), ширина, высота, толщина стены в проёме. Принято в проекте: входная дверь: положение и ширина проёма — по брифу заказчика, не замерены.	Архитектор	±5 мм	Проёмы на обмерном плане и в ведомости проёмов; привязки мебели и выводов к проёмам. Листы: л. 13 — Обмерный план л. 15 — План дверей и ведомость заполнения проёмов	акт контрольного обмера; фото с рулеткой и привязкой к стене или углу	К-1 Результат принимает: Архитектор

Этап 2. После демонтажа, до черновых работ

№	Где	Способ	Что сделать	Кто выполняет	Точность	Что пересчитается в альбоме	Чем подтверждается	Закрывает вопросы реестра
О-15	Гостиная-кухня (пом. 1), Спальня (пом. 2), Детская (пом. 3), Санузел (пом. 4), Прихожая (пом. 5)	Обмер	Нивелировка плиты перекрытия и существующего пола после демонтажа покрытий: отметки в углах и по сетке, перепады по помещению, уклоны, отметки порогов (чистый пол в мокрых зонах принят -15 мм, 0 мм). Принятая толщина стяжки 33 мм, 50 мм и отметка чистого пола — расчётные, не от замера плиты.	Архитектор	±5 мм по отметке; ровность просвет под 2-метровой рейкой, горизонталь против 0,2 % длины помещения	Толщина стяжки и отметка чистого пола; уклоны к трапам и пороги; выпуски К1 относительно чистого пола (план разводки); объёмы стяжки и смеси в ВОР и спецификации. Листы: л. 40, 43 — План полов л. 32 — Схема разводки водопровода и канализации	акт контрольного обмера	Вопроса в реестре нет: Альбом принимает отметки плиты и толщину пирога пола без нивелировки. Результат принимает: Отделочник
О-16	Гостиная-кухня (пом. 1), Спальня (пом. 2), Детская (пом. 3), Санузел (пом. 4), Прихожая (пом. 5)	Обмер	Вертикаль и плоскостность стен: отклонение от вертикали по высоте стены (отвес или лазерный уровень), просвет под правилом 2 м, кривизна углов. Нужно там, где от стены зависит изделие: облицовка плиткой (пом. 4), штукатурка и окраска (пом. 1, 2, 3, 4, 5), встроенная мебель и кухня (пом. 1, 2, 3, 5).	Архитектор	до 1 мм на 2 м (правило и клиновой щуп); вертикаль — мм на высоту стены, отклонения подписываются на плане	Толщина штукатурки и расход смеси в ВОР и спецификации; раскладка плитки (подрезка у стен); зазоры и крепление встроенной мебели и кухни. Листы: л. 40–42 — Раскладка плитки л. 44 — Ведомость отделки помещений	акт контрольного обмера	Вопроса в реестре нет: Альбом принимает стены ровными и вертикальными без замера. Результат принимает: Отделочник

Допущения и предложения на листе

Основа листа: размеры помещений и положение проёмов введены заказчиком в брифе, на объекте не замерены (К-1); высота потолка 2700 мм — по брифу заказчика, не замерена (К-2); толщины стен приняты по брифу: наружные 200 мм, внутренние 150 мм — не обмерены (К-1); тип дома монолитный, перекрытие 200 мм — по брифу заказчика, документов нет (К-3); планировка (стены, проёмы, объединение кухни и гостиной, расширение санузла) — по брифу без обмера и плана БТИ (К-7); разрешённая мощность 10 кВт принята, ТУ не переданы (К-8); вентканалы приняты, в брифе не заданы (К-9); подрайон климата не задан — принят не северный (жилые от 2,5 м) (К-10).

См. лист открытых вопросов (лист 5, записи К-1–К-3, К-7–К-10).

Изм.	Кол.уч	Лист	№ док.	Подп.	Дата
Разраб.		Кырлан А.С.			21.10.26
Пров.					
ГИП					
Н. контр.					
Утв.					

ГД-2026-011-АИ

Квартира 56 м²

ЖК «Северный парк», Москва

Дизайн-проект интерьера

Стадия	Лист	Листов
РП	8	83

Задание на контрольный обмер и обследование.
Лист 3 из 4
М б/м

Кырлан Александр Сергеевич

Задание на контрольный обмер и обследование. Лист 4 из 4

ПРЕДВАРИТЕЛЬНО · не для производства работ · открыто пунктов: 10 (реестр — л. 5)

Что замерить, вскрыть и получить до заказа материалов и изделий

Документы и данные закупки (не на объекте)

№	У кого, откуда	Способ	Что получить	К какому сроку	Что пересчитается в альбоме	Чем подтверждается	Закрывает вопросы реестра
О-17	Заказчик; управляющая компания или застройщик	Документ	Проект дома (разделы АР и КР) или план БТИ с указанием несущих конструкций; тип дома и конструкция перекрытия.	До начала демонтажных работ	Несущие стены на обмерном плане и плане демонтажа; допустимость демонтажа и новых проёмов; нагрузки от перегородок. Листы: л. 13 — Обмерный план л. 14 — План демонтажа и монтажа перегородок	копия документа	К-3 Результат принимает: Архитектор
О-18	вся квартира	Документ	Поэтажный план БТИ с экспликацией.	до демонтажа	обмерный план, план демонтажа и монтажа, расстановка мебели Листы: л. 13 — Обмерный план л. 14 — План демонтажа и монтажа перегородок л. 17 — План расстановки мебели	копия документа	К-7 Результат принимает: Архитектор
О-19	заказчик, УК	Документ	ТУ на электроснабжение или справка УК о разрешённой мощности и вводном автомате.	до сборки щита	вводной автомат, группы варочной панели и духового шкафа Листы: л. 26 — Однолинейная схема щита	копия документа	К-8 Результат принимает: Инженер-электрик
О-20	адрес объекта, СП 131.13330	Документ	Климатический подрайон по СП 131.13330 (по адресу объекта)	до заказа каркаса потолков	план потолков, разрезы, ведомость объёмов Листы: л. 36 — План потолков	копия документа	К-10 Результат принимает: Архитектор

Примечания

1. Подтверждение: акт контрольного обмера (дата, кто присутствовал, прибор, перечень промеров с результатами, подписи присутствующих); к акту — фото вскрытий и узлов и техническое заключение организации, выполнившей обследование.
2. Номера листов — по ведомости рабочих чертежей комплекта (лист «Общие данные»).
3. Пункт исключается из задания при следующем выпуске, когда акт подписан, значение внесено в проект и листы перевыпущены; знак «*» у величины снимается только замером.

Допущения и предложения на листе

Основа листа: размеры помещений и положение проёмов введены заказчиком в брифе, на объекте не замерены (К-1); высота потолка 2700 мм — по брифу заказчика, не замерена (К-2); толщины стен приняты по брифу: наружные 200 мм, внутренние 150 мм — не обмерены (К-1); тип дома монолитный, перекрытие 200 мм — по брифу заказчика, документов нет (К-3); планировка (стены, проёмы, объединение кухни и гостиной, расширение санузла) — по брифу без обмера и плана БТИ (К-7); разрешённая мощность 10 кВт принята, ТУ не переданы (К-8); вентканалы приняты, в брифе не заданы (К-9); подрайон климата не задан — принят не северный (жилые от 2,5 м) (К-10).
См. лист открытых вопросов (лист 5, записи К-1–К-3, К-7–К-10).

Изм.	Кол.уч	Лист	№ док.	Подп.	Дата
Разраб.		Кырлан А.С.			21.10.26
Пров.					
ГИП					
Н. контр.					
Утв.					

ГД-2026-011-АИ

Квартира 56 м²

ЖК «Северный парк», Москва

Дизайн-проект интерьера

Стадия	Лист	Листов
РП	9	83

Задание на контрольный обмер и обследование.
Лист 4 из 4
М б/м

Кырлан Александр Сергеевич

выпуск 19.10.2026 № 1c3e34763b · стр. 11 из 117

График закупок и работ. Лист 1 из 3

ПРЕДВАРИТЕЛЬНО · не для производства работ · открыто пунктов: 10 (реестр — л. 5)

Что заказывать и когда не раньше чего: относительный порядок без дат; срок поставки — из данных или «уточняется у поставщика»

Лист не содержит дат: контрольного обмера, подписанных решений автора и договоров ещё нет, и любая дата была бы выдумана. Вместо календаря — порядок и условия: замер → решение и выбор изделия → заказ → срок поставки → работа, которую позиция блокирует.
Срок поставки печатается как срок, только если он задан в данных позиции. Нет — «срок уточняется у поставщика» и ссылка на вопрос реестра о сроках; типовой диапазон практики стоит рядом как ориентир и заказывать по нему нельзя. Номера З-N и Р-N — строки этого листа, К-N — записи реестра открытых вопросов, О-N — позиции задания на контрольный обмер.

Закупки: что заказывается, от чего зависит заказ и какую работу блокирует

№	Позиция и где	1. Замер до заказа	2. Решение, выбор изделия, паспорт	3. Условие заказа	4. Срок поставки	5. Блокирует работу	Закрывает вопросы реестра
З-1	Двери скрытого монтажа с коробом под покраску в новой перегородке П-2**: Д-4 — 1 шт. пом. 3	О-13: обмер: Детская (пом. 3): окно пом. 3, стена В (К-1) О-3: обмер: Вся квартира, все помещения; обход по часовой стрелке от входа (К-1)	Новые перегородки заданы заказчиком в брифе положением, материалом и толщиной; конструкция (система, число слоёв, каркас, звукоизоляция, Rw) выбрана исполнителем по каталогам. (К-5)	После 1 и 2 и после получения срока у поставщика (вопроса о сроках нет); дата заказа — когда срок известен, не позднее чем за срок до начала Р-3.	срок уточняется у поставщика Ориентир практики (не срок поставщика): ≈ 30 дн.	Р-3 «перегородки ГКЛ»: коробку ставят в каркас перегородки до обшивки (работа по перегородкам); полотно навешивают после чистовой отделки стен	К-1, К-5
З-2	Двери скрытого монтажа с коробом под покраску в существующих проёмах: Д-2, Д-3, Д-5 — 3 шт. пом. 1, 2, 4	О-11: обмер: Гостиная-кухня (пом. 1): окно пом. 1, стена А, дверь пом. 1, стена В (К-1) О-12: обмер: Спальня (пом. 2): окно пом. 2, стена А, дверь пом. 2, стена В (К-1) О-3: обмер: Вся квартира, все помещения; обход по часовой стрелке от входа (К-1)		После 1 и 2 и после получения срока у поставщика (вопроса о сроках нет); дата заказа — когда срок известен, не позднее чем за срок до начала Р-6.	срок уточняется у поставщика Ориентир практики (не срок поставщика): ≈ 30 дн.	Р-6 «штукатурка»: короб ставят до штукатурки (коробку ставят на черновой стадии; полотно навешивают после чистовой отделки стен)	К-1
З-3	Кухонный гарнитур по проекту кухни: модули Кх1, Кх2, Кх3, Кх4, Кх5, Кх6, Кх7, Кх8, Кх9, Кх10 пом. 1			После 1 и 2 и после получения срока у поставщика (вопроса о сроках нет); дата заказа — когда срок известен, не позднее чем за срок до начала Р-16.	срок уточняется у поставщика Ориентир практики (не срок поставщика): 4–8 нед. от замера	Р-16 «кухня и мебель»: замер кухни — по готовым стенам после штукатурки или плитки, до чистового пола; производство идёт параллельно со стяжкой и отделкой	
З-4	Встраиваемая техника кухни: Кх1 холодильник, Кх6 посудомоечная машина, Кх8 вытяжка пом. 1			После 1 и 2 и после получения срока у поставщика (вопроса о сроках нет); дата заказа — когда срок известен, не позднее чем за срок до начала Р-16.	срок уточняется у поставщика	Р-16 «кухня и мебель»: паспорта и монтажные схемы — до изготовления модулей кухни: нишу и вентзазоры задаёт модель, а не типовая схема 60 см	
З-5	Стиральная машина: Сн4 (вертикальная загрузка 400 × 600 мм — условие закупки) пом. 4			После 1 и 2 и после получения срока у поставщика (вопроса о сроках нет); дата заказа — когда срок известен, не позднее чем за срок до начала Р-5.	срок уточняется у поставщика	Р-5 «черновая сантехника»: габарит и подводка — до закрытия люка и разводки	
З-6	Сантехнические приборы и инсталляции: П1, Сн1, Сн2, Сн3 пом. 1, 4	О-6: обмер: Санузел (пом. 4): Ст К1-1*, Ст В1-1; наличие стояка ГВС, арматуры и счётчиков — по всей квартире (К-4) О-2: обмер: Гостиная-кухня (пом. 1), Спальня (пом. 2), Детская (пом. 3); у окон	Новые перегородки заданы заказчиком в брифе положением, материалом и толщиной; конструкция (система, число слоёв, каркас, звукоизоляция, Rw) выбрана исполнителем по каталогам. (К-5)	После 1 и 2 и после получения срока у поставщика (вопроса о сроках нет); дата заказа — когда срок известен, не позднее чем за срок до начала Р-5.	срок уточняется у поставщика	Р-5 «черновая сантехника»: инсталляцию ставят до обшивки ГКЛВ и до гидроизоляции стены	К-4, К-5
З-7	Керамогранит и плитка: 4 поз. по артикулу и формату, 35,94 м² по раскладке пом. 1, 4, 5	О-15: обмер: Гостиная-кухня (пом. 1), Спальня (пом. 2), Детская (пом. 3), Санузел (пом. 4), Прихожая (пом. 5) О-16: обмер: Гостиная-кухня (пом. 1), Спальня (пом. 2), Детская (пом. 3), Санузел (пом. 4), Прихожая (пом. 5)		После 1 и 2 и после получения срока у поставщика (вопроса о сроках нет); дата заказа — когда срок известен, не позднее чем за срок до начала Р-10.	срок уточняется у поставщика	Р-10 «плитка»: калибр партии измеряют до раскладки, раскладку пересчитывают до заказа	
З-8	Покрытие пола (доска) и плинтус: пом. 1, 2, 3 пом. 1, 2, 3	О-15: обмер: Гостиная-кухня (пом. 1), Спальня (пом. 2), Детская (пом. 3), Санузел (пом. 4), Прихожая (пом. 5)		После 1 и 2 и после получения срока у поставщика (вопроса о сроках нет); дата заказа — когда срок известен, не позднее чем за срок до начала Р-13.	срок уточняется у поставщика	Р-13 «чистовые полы»: артикул и партия — до заказа; доску привозят к чистовым полам	

Допущения и предложения на листе

Основа листа: размеры помещений и положение проёмов введены заказчиком в брифе, на объекте не замерены (К-1); высота потолка 2700 мм — по брифу заказчика, не замерена (К-2); толщины стен приняты по брифу: наружные 200 мм, внутренние 150 мм — не обмерены (К-1); тип дома монолитный, перекрытие 200 мм — по брифу заказчика, документов нет (К-3); планировка (стены, проёмы, объединение кухни и гостиной, расширение санузла) — по брифу без обмера и плана БТИ (К-7); разрешённая мощность 10 кВт принята, ТУ не переданы (К-8); вентканалы приняты, в брифе не заданы (К-9); подрайон климата не задан — принят не северный (жилые от 2,5 м) (К-10).
Знак «*» — принято, не замерено и не подтверждено (замерить на объекте): К-4: Ст К1-1 — положение стояка канализации — по брифу заказчика, не замерено.
Знак «**» — предложение проектировщика, заказчиком не утверждено (согласовать с заказчиком): К-5: П-2 — положение, материал (ГКЛ) и толщина 150 мм — по брифу заказчика; конструкция (система С112, 2 слоя с каждой стороны, Rw 51 дБ — нижняя граница диапазона системы С112 (51–56 дБ)) — выбор исполнителя, автором не утверждена.
См. лист открытых вопросов (лист 5, записи К-1–К-5, К-7–К-10).

Изм.	Кол.уч	Лист	№ док.	Подп.	Дата
Разраб.		Кырлан А.С.			21.10.26
Пров.					
ГИП					
Н. контр.					
Утв.					

ГД-2026-011-АИ

Квартира 56 м²

ЖК «Северный парк», Москва

Дизайн-проект интерьера

Стадия	Лист	Листов
РП	10	83

График закупок и работ. Лист 1 из 3

М б/м

Кырлан Александр Сергеевич

выпуск 19.10.2026 № 1c3e34763b · стр. 12 из 117

График закупок и работ. Лист 2 из 3

Что заказывать и когда не раньше чего: относительный порядок без дат; срок поставки — из данных или «уточняется у поставщика»

Закупки: что заказывается, от чего зависит заказ и какую работу блокирует (продолжение)

№	Позиция и где	1. Замер до заказа	2. Решение, выбор изделия, паспорт	3. Условие заказа	4. Срок поставки	5. Блокирует работу	Закрывает вопросы реестра
З-9	Встроенная мебель по замеру цеха: Сп4, Дт2, Пр1 пом. 2, 3, 5	О-3: обмер: Вся квартира, все помещения; обход по часовой стрелке от входа (К-1)		После 1 и 2 и после получения срока у поставщика (вопроса о сроках нет); дата заказа — когда срок известен, не позднее чем за срок до начала Р-16.	срок уточняется у поставщика Ориентир практики (не срок поставщика): 4–8 нед. от замера	Р-16 «кухня и мебель»: цех замеряет по готовым стенам; производство 4–8 недель идёт параллельно с отделкой	К-1

Работы: порядок и что не даёт начать

№	Работа (стадия технологической последовательности)	После	Что должно быть к началу: условия и закупки	Не начинать, пока открыто в реестре
Р-1	Демонтаж покрытий, отделки стен и потолков, дверных блоков и приборов; конструкции, стены и перегородки не трогать до технического заключения (стадия 1)		до начала: запрошены документы на дом и БТИ; контрольный обмер до демонтажа (что видно) сделан	
Р-2	Контрольный обмер на голых стенах и обследование (задание — лист «Задание на контрольный обмер») (стадия 2)	Р-1	после снятия отделки: видны стояки, каналы, щиток, толщины стен; до заказа всего, что делают по размеру	
Р-3	Перегородки и фальш-стены ГКЛ: разметка, каркас, обшивка (стадия 3)	Р-2	до начала: решение по нише санузла 2 принято автором; разметка по плану монтажа подписана; коробка скрытой двери — в каркас до обшивки Закупки к началу: З-1 (двери скрытого монтажа)	К-1: Размеры помещений, толщины стен (наружные 200 мм, перегородки 150 мм) и положение проёмов введены заказчиком в бриф заказчика (site-brief-wizard, 01.08.2026): контрольный обмер на объекте не выполнялся, обмерного плана и плана БТИ в материалах нет; площадь по брифу 56 м², сумма помещений по чистым размерам брифа 56.37 м². К-3: Тип дома (монолитный) и толщина перекрытия 200 мм указаны заказчиком в брифе; проект дома, план БТИ и техническое заключение о несущих конструкциях не переданы. К-5: Новые перегородки заданы заказчиком в брифе положением, материалом и толщиной; конструкция (система, число слоёв, каркас, звукоизоляция, Rw) выбрана исполнителем по каталогам.
Р-4	Черновая электрика: штробы, короба, гофра, подрозетники, щит (стадия 4)	Р-2, Р-3	до начала: план электрики с высотами утверждён; штробы в стенах — только после технического заключения; мебель расставлена	К-8: Разрешённая мощность квартиры по ТУ в брифе не указана; принята 10 кВт (квартира с электроплитой, монолитный дом).
Р-5	Черновая сантехника и вентиляция: разводка, выводы, инсталляции, короба стояков (стадия 5)	Р-2, Р-3	до начала: положение стояков замерено; модели инсталляций и машины выбраны (габариты рамы, подводка); инсталляцию ставят до обшивки ГКЛВ и до гидроизоляции Закупки к началу: З-5 (стиральная машина), З-6 (сантехника)	К-4: Положение и диаметры стояков (канализации, холодной воды) указаны заказчиком в брифе, не замерены; врезки, краны и счётчики не описаны. К-5: Новые перегородки заданы заказчиком в брифе положением, материалом и толщиной; конструкция (система, число слоёв, каркас, звукоизоляция, Rw) выбрана исполнителем по каталогам.
Р-6	Коробки скрытых дверей, затем штукатурка стен и откосов (стадия 6)	Р-3, Р-4, Р-5	до начала: электрика и сантехника смонтированы, штробы заделаны; коробки скрытых дверей установлены до штукатурки (поэтому заказ дверей — раньше работы) Закупки к началу: З-2 (двери скрытого монтажа)	К-1: Размеры помещений, толщины стен (наружные 200 мм, перегородки 150 мм) и положение проёмов введены заказчиком в бриф заказчика (site-brief-wizard, 01.08.2026): контрольный обмер на объекте не выполнялся, обмерного плана и плана БТИ в материалах нет; площадь по брифу 56 м², сумма помещений по чистым размерам брифа 56.37 м².
Р-7	Стяжка пола и тёплый пол (стадия 7)	Р-6	до начала: штукатурка сделана; трубы под стяжкой приняты; нивелировка плиты выполнена	
Р-8	Гидроизоляция санузлов и тест проливом (стадия 8)	Р-7	до начала: стяжка набрала прочность и сухая по инструкции гидроизоляции; выводы стоят на проектных отметках	
Р-9	ГКЛ: короба инсталляции и стояков, ниши, потолки (стадия 9)	Р-4, Р-5	до начала: черновые сети в зоне коробов приняты; закладные под тяжёлое и карнизы стоят; светильники выбраны (вырезы)	

Допущения и предложения на листе

Основа листа: размеры помещений и положение проёмов введены заказчиком в брифе, на объекте не замерены (К-1); высота потолка 2700 мм — по брифу заказчика, не замерена (К-2); толщины стен приняты по брифу: наружные 200 мм, внутренние 150 мм — не обмерены (К-1); тип дома монолитный, перекрытие 200 мм — по брифу заказчика, документов нет (К-3); планировка (стены, проёмы, объединение кухни и гостиной, расширение санузла) — по брифу без обмера и плана БТИ (К-7); разрешённая мощность 10 кВт принята, ТУ не переданы (К-8); вентканалы приняты, в брифе не заданы (К-9); подрайон климата не задан — принят не северный (жилые от 2,5 м) (К-10).

См. лист открытых вопросов (лист 5, записи К-1–К-3, К-7–К-10).

Изм.	Кол.уч	Лист	№ док.	Подп.	Дата
Разраб.		Кырлан А.С.			21.10.26
Пров.					
ГИП					
Н. контр.					
Утв.					

ГД-2026-011-АИ

Квартира 56 м²

ЖК «Северный парк», Москва

Дизайн-проект интерьера

Стадия	Лист	Листов
РП	11	83

График закупок и работ. Лист 2 из 3

М б/м

Кырлан Александр Сергеевич

выпуск 19.10.2026 № 1c3e34763b · стр. 13 из 117

График закупок и работ. Лист 3 из 3

ПРЕДВАРИТЕЛЬНО · не для производства работ · открыто пунктов: 10 (реестр — л. 5)

Что заказывать и когда не раньше чего: относительный порядок без дат; срок поставки — из данных или «уточняется у поставщика»

Работы: порядок и что не даёт начать (продолжение)

№	Работа (стадия технологической последовательности)	После	Что должно быть к началу: условия и закупки	Не начинать, пока открыто в реестре
Р-10	Плитка и керамогранит: стены, затем пол; фартук (стадия 10)	Р-7, Р-8, Р-9	до начала: гидроизоляция принята; плитка выбрана, калибр партии измерен, раскладка пересчитана и подписана Закупки к началу: З-7 (плитка)	
Р-11	Шпаклёвка стен и потолков под окраску (стадия 11)	Р-6, Р-9, Р-10	до начала: плитка готова (грязные работы закончены); штукатурка и ГКЛ сухие	
Р-12	Окраска стен, потолков, откосов (стадия 13)	Р-11	до начала: шпаклёвка отшлифована и огрунтована; выкрасы утверждены, колеровка одной партией	
Р-13	Чистовые полы: инженерная доска (стадия 14)	Р-10, Р-12	до начала: влажность основания в норме, мокрые работы закончены; доска выбрана и привезена Закупки к началу: З-8 (доска и плинтус)	
Р-14	Полотна межкомнатных дверей, плинтусы, пороги (стадия 15)	Р-12, Р-13	до начала: чистовой пол уложен; полотна скрытых дверей — после чистовой отделки стен	
Р-15	Чистовая электрика и сантехника: механизмы, светильники, смесители, приборы (стадия 16)	Р-12, Р-14	до начала: отделка готова; механизмы, светильники и приборы выбраны и привезены	
Р-16	Кухня, встроенная и корпусная мебель, бытовая техника (стадия 17)	Р-14, Р-15	до начала: чистовая сантехника и электрика подведены к местам мебели; замер кухни снят по готовым стенам (после штукатурки или плитки, до чистового пола) Закупки к началу: З-3 (кухонный гарнитур), З-4 (техника кухни), З-9 (мебель по замеру)	К-1: Размеры помещений, толщины стен (наружные 200 мм, перегородки 150 мм) и положение проёмов введены заказчиком в бриф заказчика (site-brief-wizard, 01.08.2026): контрольный обмер на объекте не выполнялся, обмерного плана и плана БТИ в материалах нет; площадь по брифу 56 м², сумма помещений по чистым размерам брифа 56.37 м².
Р-17	Сдача: осмотр по чек-листу, дефектная ведомость, устранение замечаний (стадия 18)	Р-15, Р-16	до начала: всё смонтировано; акты скрытых работ подписаны	

Примечания

1. Порядок работ — стадии технологической последовательности из 17 позиций, присутствующих в этом проекте (по строкам ведомости объёмов); остальные стадии таблицы knowledge/remont-tehnologiya.md в проекте не встречаются. Длительности работ не печатаются: их нет ни в данных, ни в нормах для этого объекта.
2. Типовые сроки — ориентир практики, не срок поставщика: скрытые двери — короб около 10 дн., полотно под покраску до 3 нед., шпон 4–5 нед., в среднем около 30 дн. (knowledge/workers/foreman.md, п. 2.4 (profil-doors)); кухня и корпусная мебель — 4–8 недель от замера (knowledge/remont-tehnologiya.md, разд. 2; knowledge/workers/foreman.md, п. 2.4). Заказ по ориентиру не назначается: срок получают у поставщика (вопрос реестра), после чего заказ планируют «не позднее чем за срок до начала работы».
3. Условия заказа берутся из реестра открытых вопросов и задания на контрольный обмер: позиция заказывается, когда закрыты замер (графа 1) и решение (графа 2). Закрывать их может только факт или решение автора с подписью; снять строку с листа можно только закрыв запись реестра.
4. Заказ по размеру до контрольного обмера не делают: двери, кухня и встроенная мебель зависят от обмера (К-11, К-13); скрытые двери, кроме того, зависят от решения по нише санузла 2 (проём Д-5 в перегородке П-1**).
5. Номера листов — по ведомости рабочих чертежей комплекта (лист «Общие данные»).

Допущения и предложения на листе

Основа листа: размеры помещений и положение проёмов введены заказчиком в брифе, на объекте не замерены (К-1); высота потолка 2700 мм — по брифу заказчика, не замерена (К-2); толщины стен приняты по брифу: наружные 200 мм, внутренние 150 мм — не обмерены (К-1); тип дома монолитный, перекрытие 200 мм — по брифу заказчика, документов нет (К-3); планировка (стены, проёмы, объединение кухни и гостиной, расширение санузла) — по брифу без обмера и плана БТИ (К-7); разрешённая мощность 10 кВт принята, ТУ не переданы (К-8); вентканалы приняты, в брифе не заданы (К-9); подрайон климата не задан — принят не северный (жилые от 2,5 м) (К-10).

Знак «**» — предложение проектировщика, заказчиком не утверждено (согласовать с заказчиком): К-5: П-1 — положение, материал (пеноблок) и толщина 100 мм — по брифу заказчика; конструкция (кладка, армирование, штукатурка) — выбор исполнителя, автором не утверждена; кладка — не ГКЛ: каркас, листы и Rw системы не считаются (система, лист, слои, Rw — «—»).

См. лист открытых вопросов (лист 5, записи К-1–К-3, К-5, К-7–К-10).

Изм.	Кол.уч	Лист	№ док.	Подп.	Дата
Разраб.		Кырлан А.С.			21.10.26
Пров.					
ГИП					
Н. контр.					
Утв.					

ГД-2026-011-АИ

Квартира 56 м²

ЖК «Северный парк», Москва

Дизайн-проект интерьера

Стадия	Лист	Листов
РП	12	83

График закупок и работ. Лист 3 из 3

М б/м

Кырлан Александр Сергеевич

выпуск 19.10.2026 № 1c3e34763b · стр. 14 из 117

01

Архитектурные решения


Кырлан Александр Сергеевич

выпуск 19.10.2026 № 1c3e34763b · стр. 15 из 117

Обмерный план

Существующее положение · размеры в мм · отметки от чистого пола

ПРЕДВАРИТЕЛЬНО · не для производства работ · открыто пунктов: 10 (реестр — л. 5)

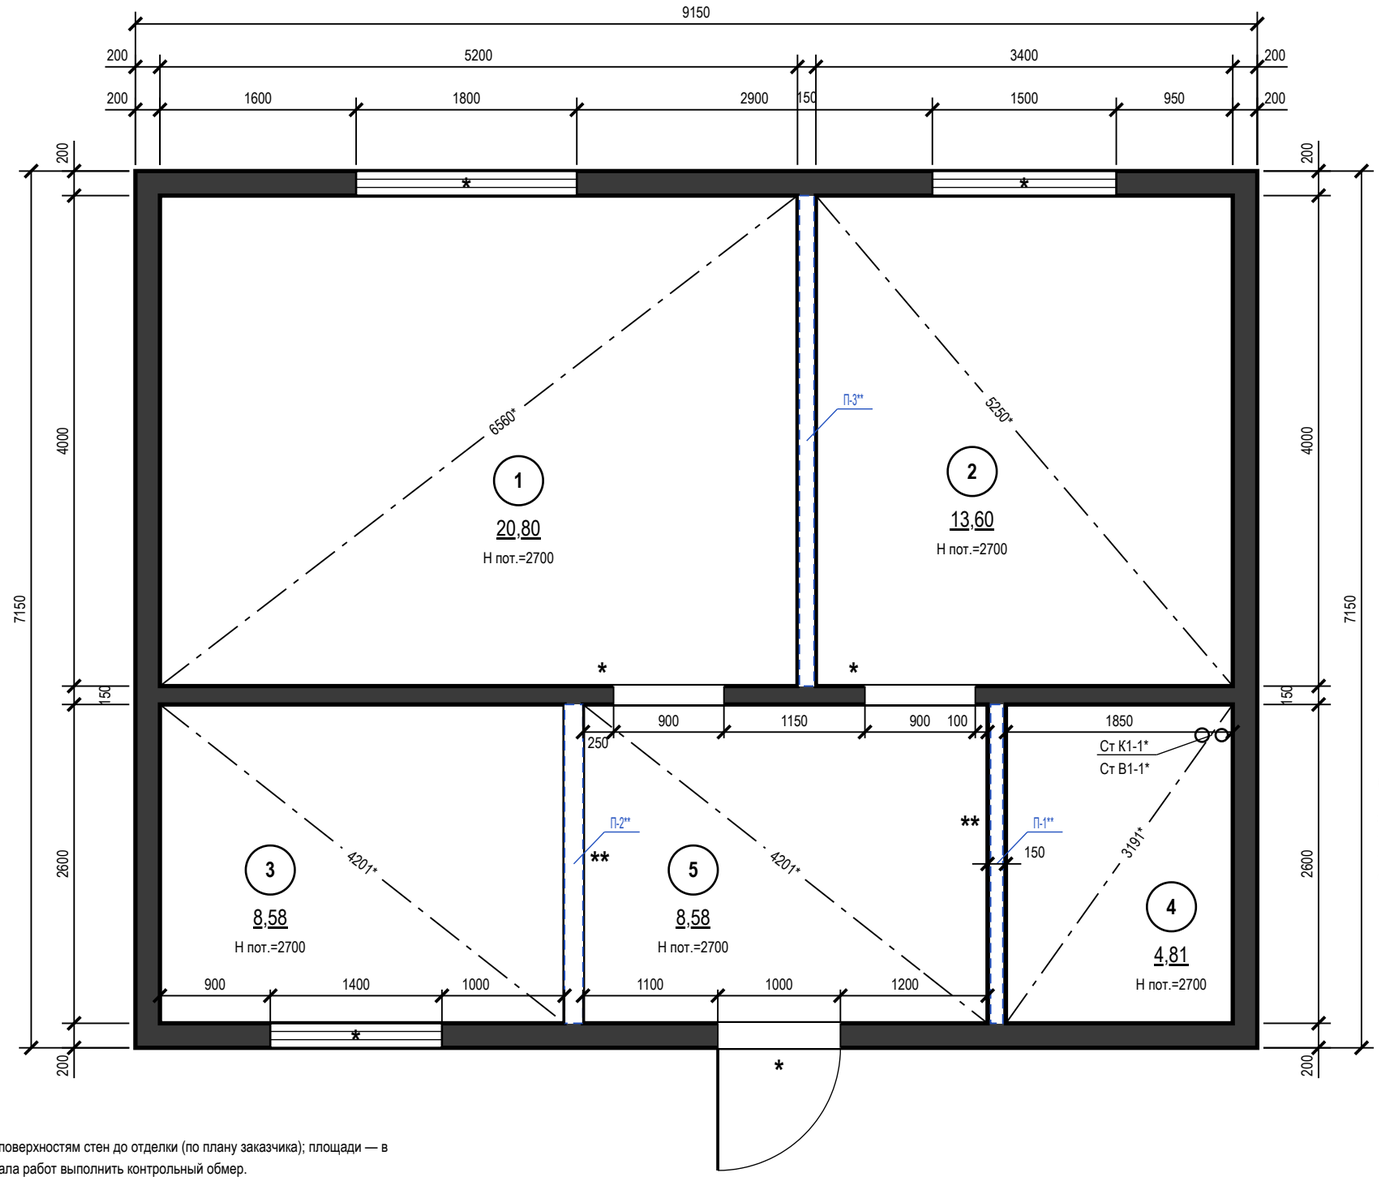

Экспликация помещений

№	Наименование	Площадь, м²
1	Гостиная-кухня	20,80
2	Спальня	13,60
3	Детская	8,58
4	Санузел	4,81
5	Прихожая	8,58
	Итого (общая площадь)	**56,37**

Условные обозначения

- существующие стены (сечение)
- окно (рама, остекление)
- проём существующий, без заполнения (откосы)
- стояк: К1 — канализация, В1 — ХВС, Т3 — ГВС
- проектная конструкция — на объекте её нет (контур)
- ** — «**» — предложение проектировщика, заказчиком не утверждено
- диагональ помещения — контроль прямоугольности
- 1 — номер помещения, площадь м²
- * — «*» — принято, не замерено и не подтверждено

Отметки по высоте

±0,000	чистый пол пом. 1–3, 5; отсчёт высот
−0,015	чистый пол пом. 4, ниже на 15 мм
−0,064*	верх плиты — расчёт, не замер (задание на обмер)
сущ. пол	снимается до плиты; не замерен (задание на обмер)

Допущения и предложения на листе. Основа листа: размеры помещений и положение проёмов введены заказчиком в брифе, не замерены (К-1); высота потолка 2700 мм — по брифу заказчика, не замерена (К-2); толщины стен приняты по брифу: наружные 200 мм, внутренние 150 мм — не обмерены (К-1); тип дома монолитный, перекрытие 200 мм — по брифу заказчика, документов нет (К-3); планировка (стены, проёмы, объединение кухни и гостиной, расширение санузла) — по брифу без обмера и плана БТИ (К-7); разрешённая мощность 10 кВт принята, ТУ не переданы (К-8); вентканалы приняты, в брифе не заданы (К-9); подрайон климата не задан — принят не северный (жилые от 2,5 м) (К-10). Знак «*» — принято, не замерено (замерить): К-4: Ст К1-1, Ст В1-1. Знак «**» — предложено, не утверждено (согласовать): К-5: П-1, П-2, П-3. См. лист открытых вопросов (лист 5, записи К-1–К-5, К-7–К-10).

Примечания

1. Размеры — в мм по чистым поверхностям стен до отделки (по плану заказчика); площади — в м² по тем же размерам. До начала работ выполнить контрольный обмер.
2. Знак «*» у проёма — положение не замерено; реестр: лист 5, вопрос К-1.
3. Знак «*» у стояка — положение принято, не замерено (все стояки); сверить на объекте до разметки. Реестр: лист 5, вопрос К-4.
4. За отметку ±0,000 принят чистый пол, не существующий (блок отметок). Н пот. — высота от чистого пола до плиты перекрытия.
5. Толщины стен: наружные 200 мм, перегородки 150 мм; отличающиеся толщины и уступы размерами на плане.
6. Несущие стены не определены: до технического заключения все стены считать несущими; проёмы и штробы в них не выполнять.
7. Дверные проёмы показаны без заполнения (двери — лист 15); высота дверных проёмов 2100 мм; низ окон (подоконник) 850, 900 мм от чистого пола, высота окон 1500, 1450 мм.
8. Диагонали — контрольные размеры; «*» — расчёт по принятому контуру (К-1), при обмере заменить замеренным; расхождение более 5 мм подписать на плане как перекос.
9. Размеры проверить на месте до начала работ; расхождение контрольных промеров ≤ 2 %.

Принято, не определено или спорно

полностью — лист 5

К-2 — Высота потолка 2700 мм указана заказчиком в брифе, на объекте не замерена

К-3 — Тип дома (монолитный) и толщина перекрытия 200 мм указаны заказчиком в брифе; проект дома, план БТИ и техническое заключение о несущих конструкциях не переданы

К-7 — Планировка принята по брифу заказчика: положение существующих стен и проёмов, объединение кухни с гостиной (демонтаж С-1), расширение санузла (демонтаж С-2, перегородка П-1**) введены в мастер брифа без обмерного плана и плана БТИ

1000 мм · печать 1:1

Изм.	Кол.уч	Лист	№ док.	Подп.	Дата
Разраб.		Кырлан А.С.			21.10.26
Пров.					
ГИП					
Н. контр.					
Утв.					

ГД-2026-011-АИ

Квартира 56 м²

ЖК «Северный парк», Москва

Дизайн-проект интерьера

Стадия	Лист	Листов
РП	13	83

Обмерный план

М 1:50

Кырлан Александр Сергеевич


выпуск 19.10.2026 № 1c3e34763b · стр. 16 из 117

План демонтажа и монтажа перегородок

Существующее — серым, демонтаж — красным, монтаж — синим · размеры в мм

ПРЕДВАРИТЕЛЬНО · не для производства работ · открыто пунктов: 10 (реестр — л. 5)

Допущения и предложения на листе. Основа листа: размеры помещений и положение проёмов введены заказчиком в брифе, не замерены (К-1); высота потолка 2700 мм — по брифу заказчика, не замерена (К-2); толщины стен приняты по брифу: наружные 200 мм, внутренние 150 мм — не обмерены (К-1); тип дома монолитный, перекрытие 200 мм — по брифу заказчика, документов нет (К-3); планировка (стены, проёмы, объединение кухни и гостиной, расширение санузла) — по брифу без обмера и плана БТИ (К-7); разрешённая мощность 10 кВт принята, ТУ не переданы (К-8); вентканалы приняты, в брифе не заданы (К-9); подрайон климата не задан — принят не северный (жилые от 2,5 м) (К-10). Знак «*» — принято, не замерено (замерить). Знак «**» — предложено, не утверждено (согласовать): К-5: П-1, П-2, П-3. См. лист открытых вопросов (лист 5, записи К-1–К-3, К-5, К-7–К-10).

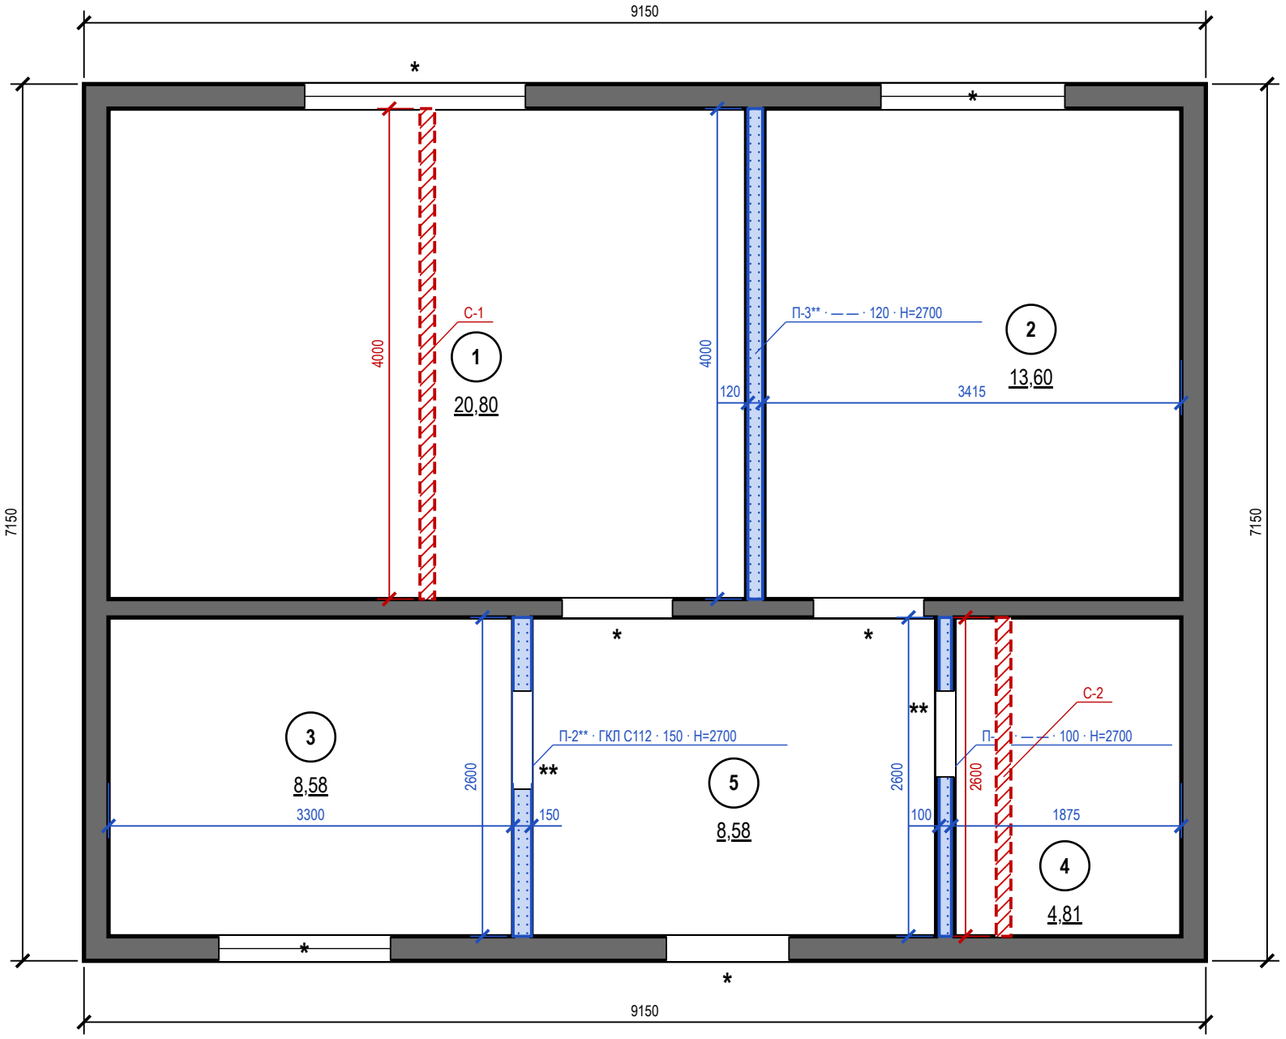


Ведомость демонтажа и монтажа

Марка	Конструкция	Длина, мм	Толщ., мм	Высота	Примечание
С-1	демонтаж: перегородка	4000	120	2700	перегородка кухня/гостиная, объединение в кухню-гостиную
С-2	демонтаж: перегородка	2600	120	2700	старая стена санузла, расширение мокрой зоны
П-1**	монтаж: Пеноблок D500, армирование через 2 ряда, штукатурка с двух сторон,	2600	100	Н=2700	новая стена санузла, пеноблок под гидроизоляцию
П-2**	монтаж: ГКЛ 12,5 мм в 2 слоя с каждой стороны по металлическому каркасу ПС/ПН, минеральная вата 50 мм, С112	2600	150	Н=2700	перегородка детская/прихожая, ГКЛ со звукоизоляцией
П-3**	монтаж: Кирпич керамический полнотелый на ребро, штукатурка с двух сторон,	4000	120	Н=2700	перегородка спальня/гостиная, кирпич для звукоизоляции

Условные обозначения

- существующие стены — сохраняются; несущие не определены — считать несущими
- демонтируемые конструкции (красным)
- новое — возводится по проекту (синим)
- ** — «**» — предложение проектировщика, заказчиком не утверждено
- проём существующий, без заполнения (откосы)
- 1 — номер помещения, площадь м²
- * — «*» — принято, не замерено и не подтверждено

Отметки по высоте

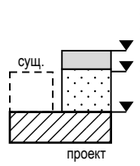

±0,000	чистый пол пом. 1–3, 5; отсчёт высот
−0,015	чистый пол пом. 4, ниже на 15 мм
−0,064*	верх плиты — расчёт, не замер (задание на обмер)
сущ. пол	снимается до плиты; не замерен (задание на обмер)

Примечания

1. Демонтаж несущих стен и плит перекрытия не производится; снос несущих конструкций — только по техническому заключению (в ведомости).
2. Новые перегородки и фальш-стены (синим) привязаны от капитальных стен и наружного контура; высота — по ведомости («до плиты» — до низа плиты перекрытия); проёмы в них усилить стойками каркаса.
3. Знак «**» — предложение проектировщика, заказчиком не утверждено (согласовать с заказчиком) у конструкций (вопрос К-5): до решения не возводить. На обмере они показаны контуром — на объекте их нет.
4. Перепланировку согласовать до начала работ (ЖК РФ, ст. 26); план не передавать в работу до допуска главного инженера проекта.
5. Дверные блоки — по плану дверей (лист 15); существующие проёмы не расширяются.
6. Знак «*» — положение проёма не замерено: окна пом. 1, 2, 3; двери пом. 1, 2, 5. Реестр: лист 5, вопрос К-1.
7. Демонтаж существующих покрытий пола, стен и потолка, дверных блоков и сантехприборов (если есть) — до основания; объёмы демонтажа — для справки, по факту на объекте.
8. За отметку ±0,000 принят чистый пол, не существующий (блок отметок). Размеры — в мм по чистовой поверхности стен до отделки.
9. Размеры проверить на месте до начала работ: расхождение с обмером — не более 2 % (иначе — к архитектору).
10. Несущие стены не определены: до технического заключения все стены считать несущими — проёмы, ниши и штробы в них не выполнять.

1000 мм · печать 1:1

Изм.	Кол.уч	Лист	№ док.	Подп.	Дата
Разраб.		Кырлан А.С.			21.10.26
Пров.					
ГИП					
Н. контр.					
Утв.					

ГД-2026-011-АИ

Квартира 56 м²

ЖК «Северный парк», Москва

Дизайн-проект интерьера

Стадия	Лист	Листов
РП	14	83

План демонтажа и монтажа перегородок

М 1:50


Кырлан Александр Сергеевич

выпуск 19.10.2026 № 1c3e34763b · стр. 17 из 117

План дверей и ведомость заполнения проёмов

Проёмы, марки заполнения, привязки · размеры в мм

ПРЕДВАРИТЕЛЬНО · не для производства работ · открыто пунктов: 10 (реестр — л. 5)

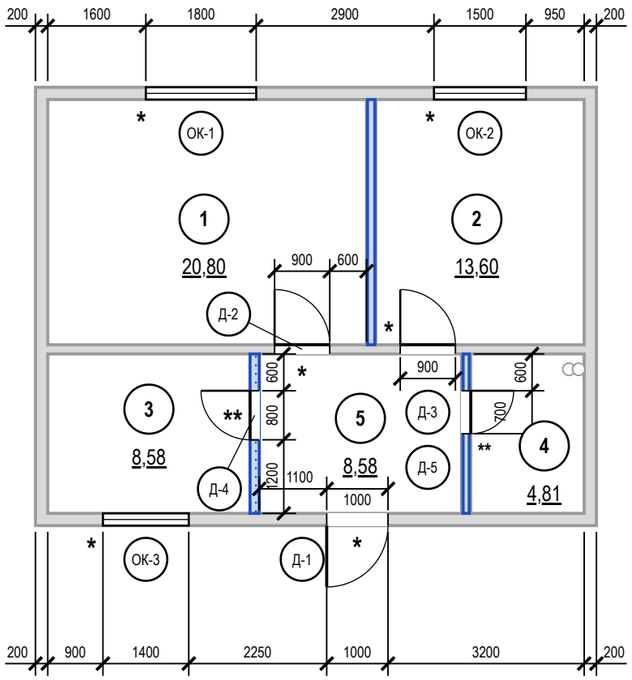

Ведомость заполнения проёмов

Марка	Наименование, обозначение	Проём ш×в, мм	Кол.	Откр.	Отделка полотна	Фурнитура	Прим.
Д-1	Блок дверной входной, ГОСТ 31173-2016	1000×2100	1	Л	в комплекте блока	в комплекте блока (замки, глазок)	* пом. 5; наружу
Д-2	Дверь скрытого монтажа, ТУ изготовителя	900×2100	1	П	окраска S 0804-Y30R с двух сторон	скрытые петли 3D, магнитный замок	* пом. 1
Д-3	Дверь скрытого монтажа, ТУ изготовителя	900×2100	1	П	окраска S 0804-Y30R с двух сторон	скрытые петли 3D, магнитный замок	* пом. 2
Д-4	Дверь скрытого монтажа, ТУ изготовителя	800×2100	1	Л	окраска S 0804-Y30R с двух сторон	скрытые петли 3D, магнитный замок	** пом. 3
Д-5	Дверь скрытого монтажа, ТУ изготовителя	700×2100	1	П	в тон облицовки — пом. 4, S 0804-Y30R — пом. 5	скрытые петли 3D, магнитный замок, фиксатор WC	** пом. 4; порог 15
ОК-1	Блок оконный, ГОСТ 23166-2021	1800×1500	1				* пом. 1; низ 850
ОК-2	Блок оконный, ГОСТ 23166-2021	1500×1450	1				* пом. 2; низ 900
ОК-3	Блок оконный, ГОСТ 23166-2021	1400×1450	1				* пом. 3; низ 900

Условные обозначения

- стены (подложка обмера)
- новое — возводится по проекту (синим)
- дверь распашная, дуга открывания
- дверь скрытого монтажа
- дверь входная (полотно толще)
- оконный блок
- Д — марка типа (Д-N, ОК-N)
- 1 — номер помещения, площадь м²
- * — «*» — принято, не замерено и не подтверждено
- ** — «**» — предложение проектировщика, заказчиком не утверждено

Примечания

1. Размеры проёмов и привязки — в миллиметрах от чистых граней стен до отделки; привязка — от угла того помещения, со стороны которого стоит размер. Размер в ведомости — ширина × высота проёма от чистого пола 0,000. Откос от угла помещения до проёма с коробкой — не менее 50 мм.
2. Марки в кружках — типы заполнения проёмов (ГОСТ 21.501-2018, п. 5.3.2); одна марка — один типоразмер; количество сверено с планом.
3. Открывание: Л — петли слева, П — справа, если смотреть со стороны, куда открывается полотно (на себя).
4. Скрытые двери (Д-2…Д-5): проём замерить в чистоте; блок заказать до штукатурки (≈ 30 дн.), короб ставить до штукатурки; полотно навесить после чистовой отделки, красить в цвет стен. Порядок практика монтажа, изготовитель подтверждает.
5. Размер в ведомости — проёма: полотно скрытой двери уже проёма на коробку и зазор 10–15 мм (модель не выбрана); Д-2, Д-3, Д-5 — существующие проёмы, до техзаключения не расширять (К-1, К-5).
6. Д-1: дуга наружу — по плану заказчика, не проверено; блок оставить или заменить — не решено (К-1).
7. Знак «*» у проёма — допущение: положение проёма не замерено (окно пом. 1, стена А; дверь пом. 1, стена В; окно пом. 2, стена А; дверь пом. 2, стена В; окно пом. 3, стена В; дверь пом. 5, стена В); размер напечатан как принятый; в ведомости — знак «*» в графе «Прим.». Реестр: лист 5, вопрос К-1.
8. Экспликация помещений — лист 13; в марках помещений — номер и площадь, м².
9. Привязка проёма к углу помещения меньше 1 мм на листе, размер на плане не показан: Д-3 — 100 мм.

Допущения и предложения на листе. Основа листа: размеры помещений и положение проёмов введены заказчиком в брифе, на объекте не замерены (К-1); высота потолка 2700 мм — по брифу заказчика, не замерена (К-2); толщины стен приняты по брифу: наружные 200 мм, внутренние 150 мм — не обмерены (К-1); тип дома монолитный, перекрытие 200 мм — по брифу заказчика, документов нет (К-3); планировка (стены, проёмы, объединение кухни и гостиной, расширение санузла) — по брифу без обмера и плана БТИ (К-7); разрешённая мощность 10 кВт принята, ТУ не переданы (К-8); вентканалы приняты, в брифе не заданы (К-9); подрайон климата не задан — принят не северный (жилые от 2,5 м) (К-10). Знак «*» — принято, не замерено и не подтверждено (замерить на объекте): К-4: Ст К1-1 — положение стояка канализации — по брифу заказчика, не замерено; Ст В1-1 — положение стояка холодной воды — по брифу заказчика, не замерено. Знак «**» — предложение проектировщика, заказчиком не утверждено (согласовать с заказчиком): К-5: П-1 — положение, материал (пеноблок) и толщина 100 мм — по брифу заказчика; конструкция (кладка, армирование, штукатурка) — выбор исполнителя, автором не утверждена; кладка — не ГКЛ: каркас, листы и Rw системы не считаются (система, лист, слои, Rw — «—»); П-2 — положение, материал (ГКЛ) и толщина 150 мм — по брифу заказчика; конструкция (система С112, 2 слоя с каждой стороны, Rw 51 дБ — нижняя граница диапазона системы С112 (51–56 дБ)) — выбор исполнителя, автором не утверждена; П-3 — положение, материал (кирпич) и толщина 120 мм — по брифу заказчика; конструкция (кладка, армирование, штукатурка) — выбор исполнителя, автором не утверждена; кладка — не ГКЛ: каркас, листы и Rw системы не считаются (система, лист, слои, Rw — «—»). См. лист открытых вопросов (лист 5, записи К-1–К-5, К-7–К-10); по листу — К-1.

1000 мм · печать 1:1

						ГД-2026-011-АИ			
						Квартира 56 м²			
Изм.	Кол.уч	Лист	№ док.	Подп.	Дата	ЖК «Северный парк», Москва			
Разраб.		Кырлан А.С.			21.10.26	Дизайн-проект интерьера	Стадия	Лист	Листов
Пров.							РП	15	83
ГИП						**План дверей и ведомость заполнения проёмов**	**Кырлан Александр Сергеевич**		
						М 1:100			
Н. контр.									
Утв.									

выпуск 19.10.2026 № 1c3e34763b · стр. 18 из 117

02

Планировочное решение

Кырлан Александр Сергеевич

выпуск 19.10.2026 № 1c3e34763b · стр. 19 из 117


Концепция интерьера

Джапанди · схема аналоговая · 60/30/10 · материалы, образы и зонирование


Идея

Джапанди для пары с ребёнком 6 лет и котом: низкая мебель, два тона дерева (дуб и тёмный ясень), матовые тёплые нейтрали, серо-зелёный второй план, одна картина на комнату. Кухня линейная у стены Г с навесными шкафами, стол у окна, ТВ-зона с низкой консолью; рабочее место в спальне; шкаф-купе и антресоль в прихожей; скрытые двери, шторы в нише потолка; без глянца и холодного белого. Стиль — джапанди: тишина, заземлённость, медленная жизнь, тёплый минимализм, ваби-саби, hygge. Стены S 0804-Y30R, потолок Damask F485, серо-зелёный Sea Smoke и дуб под маслом, акценты — олива Bancha и тёмный орех; без глянца (К-6). Цветовая схема — аналоговая, пропорция 60/30/10: база на стенах и потолках, вторичный цвет — в текстиле и мягкой мебели, акцент — точечно.

Мудборд: материалы и фактуры

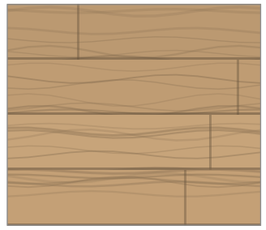

1167-1101
пол

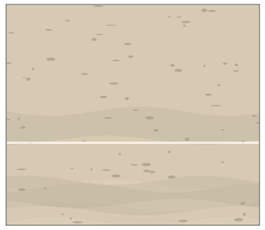

Керамогранит под травертин
фартук



Damask · Tikkurila F485
потолок



NCS S 0804-Y30R
стены, плинтус




Bancha · Farrow & Ball No. 298
акцент (стена А)




NCS S 5010-G70Y
акцент (стена А)



Sea Smoke · Tikkurila X447
акцент (стена Г)

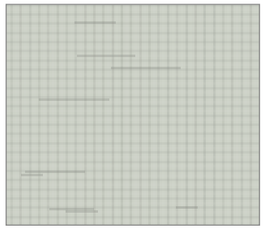

Лён, Tikkurila X447
портьеры-волна, подушки декоративные на кровать

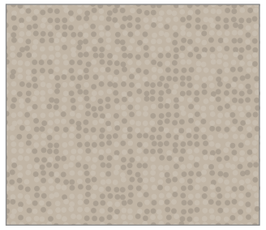


Шерсть, Tikkurila V484
ковёр в зоне отдыха, плед на диван

Палитра 60/30/10



60 % база — NCS S 0804-Y30R, LRV 78; Tikkurila F485 Damask, LRV 83; Little Greene No. 105 Slaked Lime, LRV 82
30 % вторичный — Tikkurila X447 Sea Smoke, LRV 63; Tikkurila V484 Driftwood, LRV 47; NCS S 2005-Y30R, LRV 55
10 % акцент — Farrow & Ball No. 298 Bancha, LRV 14; NCS S 5010-G70Y, LRV 22; NCS S 7005-Y20R, LRV 9

Функциональное зонирование (М 1:100)

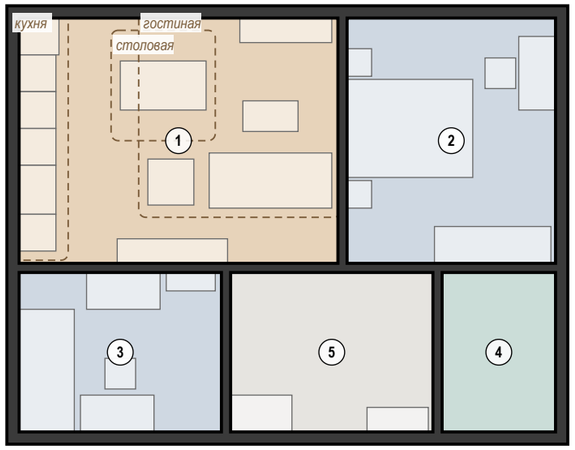

дневная зона: гостиная, кухня, столовая
ночная зона: спальни
мокрая зона: санузлы
вход и коммуникации
функциональная зона в помещении
1 номер помещения (лист 17)

Образы помещений

1. Гостиная-кухня 20,80 м²

стены NCS S 0804-Y30R; акцент No. 298 на стене А
пол — 1167-1101
текстиль: портьеры X447, тюль F485, ковёр в зоне отдыха V484
декор: картина над консолью, Фикус

2. Спальня 13,60 м²

стены NCS S 0804-Y30R; акцент S 5010-G70Y на стене А
пол — 1167-1101
текстиль: портьеры X447, тюль F485, ковёр S 2005-Y30R
декор: картина над кроватью

3. Детская 8,58 м²

стены NCS S 0804-Y30R; акцент X447 на стене Г
пол — 1167-1101
текстиль: портьеры X447, тюль F485, ковёр игровой V484
декор: картина над кроватью, зеркало в рост
свет 2700 К, сценарии: вечер

5. Прихожая 8,58 м²

стены NCS S 0804-Y30R
пол — A8UZ
декор: зеркало над скамьёй
свет 3000/2700 К

4. Санузел 4,81 м²

стены Atlas Concorde A8UZ
пол — A8UZ
декор: зеркало над умывальником
свет 3000 К

Материалы и отделка

1167-1101
пол — пом. 1, 2, 3

Керамогранит под травертин
матовый; 1200×600
фартук — пом. 1

A8UZ
пол, стены — пом. 4, 5

NCS S 0804-Y30R, LRV 78
Tikkurila Euro Power 7, колеровка по NCS, матовая
стены, плинтус — пом. 1, 2, 3, 5

Tikkurila F485 Damask, LRV 83
Tikkurila Euro Power 7, глубокоматовая
потолок — пом. 1, 2, 3, 4, 5

Farrow & Ball No. 298 Bancha, LRV 14
акцентная стена
акцент (стена А) — пом. 1

NCS S 5010-G70Y, LRV 22
акцентная стена
акцент (стена А) — пом. 2

Tikkurila X447 Sea Smoke, LRV 63
акцентная стена
акцент (стена Г) — пом. 3

Текстиль и металл

Лён, Tikkurila X447
портьеры-волна, подушки декоративные на кровать

Вуаль, Tikkurila F485
тюль

Шерсть, Tikkurila V484
ковёр в зоне отдыха, плед на диван

Букле, Tikkurila X447
подушки на диван

Бархат, Farrow & Ball No. 298
подушки на диван

Шерсть, NCS S 2005-Y30R
ковёр под кроватью

Бархат, NCS S 5010-G70Y
подушки на кровать

Шерсть, NCS S 5010-G70Y
плед на кровать

Букле, NCS S 1002-Y50R
подушки декоративные на кровать

Бархат, Tikkurila X447
подушки на кровать

Чего избегаем

1) Бежевое всё без контраста светлого и тёмного
2) Японские сувениры: веера, иероглифы, сакура-принты, катаны, Будды
3) Холодные серые, чистый белый, свет 4000 К+
4) Три-четыре породы и тона дерева, глянцевые плёнки под дерево
5) Много мелкого декора, заставленные открытые полки
6) Искусственные растения и пампасная трава как единственный декор

Допущения и предложения на листе

Основа листа: размеры помещений и положение проёмов введены заказчиком в брифе, на объекте не замерены (К-1); высота потолка 2700 мм — по брифу заказчика, не замерена (К-2); толщины стен приняты по брифу: наружные 200 мм, внутренние 150 мм — не обмерены (К-1); тип дома монолитный, перекрытие 200 мм — по брифу заказчика, документов нет (К-3); планировка (стены, проёмы, объединение кухни и гостиной, расширение санузла) — по брифу без обмера и плана БТИ (К-7); разрешённая мощность 10 кВт принята, ТУ не переданы (К-8); вентканалы приняты, в брифе не заданы (К-9); подрайон климата не задан — принят не северный (жилые от 2,5 м) (К-10).
См. лист открытых вопросов (лист 5, записи К-1–К-3, К-7–К-10).

Примечания

1. Коды цвета — по веерам производителей (колерная карта, лист 45); перед закупкой краски — выкрас на стене объекта под дневным светом и лампами проекта.
2. Материалы — по ведомости отделки (лист 44); мебель, текстиль и декор — по спецификации (лист 18). Образцы доски, керамогранита и тканей утвердить до заказа.
3. Фактуры на листе условные, цвет передан по HEX-значениям производителей: при печати возможны отклонения, решение — только по физическому образцу.

Изм.	Кол.уч	Лист	№ док.	Подп.	Дата
Разраб.		Кырлан А.С.			21.10.26
Пров.					
ГИП					
Н. контр.					
Утв.					

ГД-2026-011-АИ

Квартира 56 м²

ЖК «Северный парк», Москва

Дизайн-проект интерьера

Стадия	Лист	Листов
РП	16	83

Концепция интерьера

М б/м


Кырлан Александр Сергеевич

выпуск 19.10.2026 № 1c3e34763b · стр. 20 из 117

План расстановки мебели

Мебель и оборудование · размеры в мм от чистовых стен · марки — по ведомости

ПРЕДВАРИТЕЛЬНО · не для производства работ · открыто пунктов: 10 (реестр — л. 5)

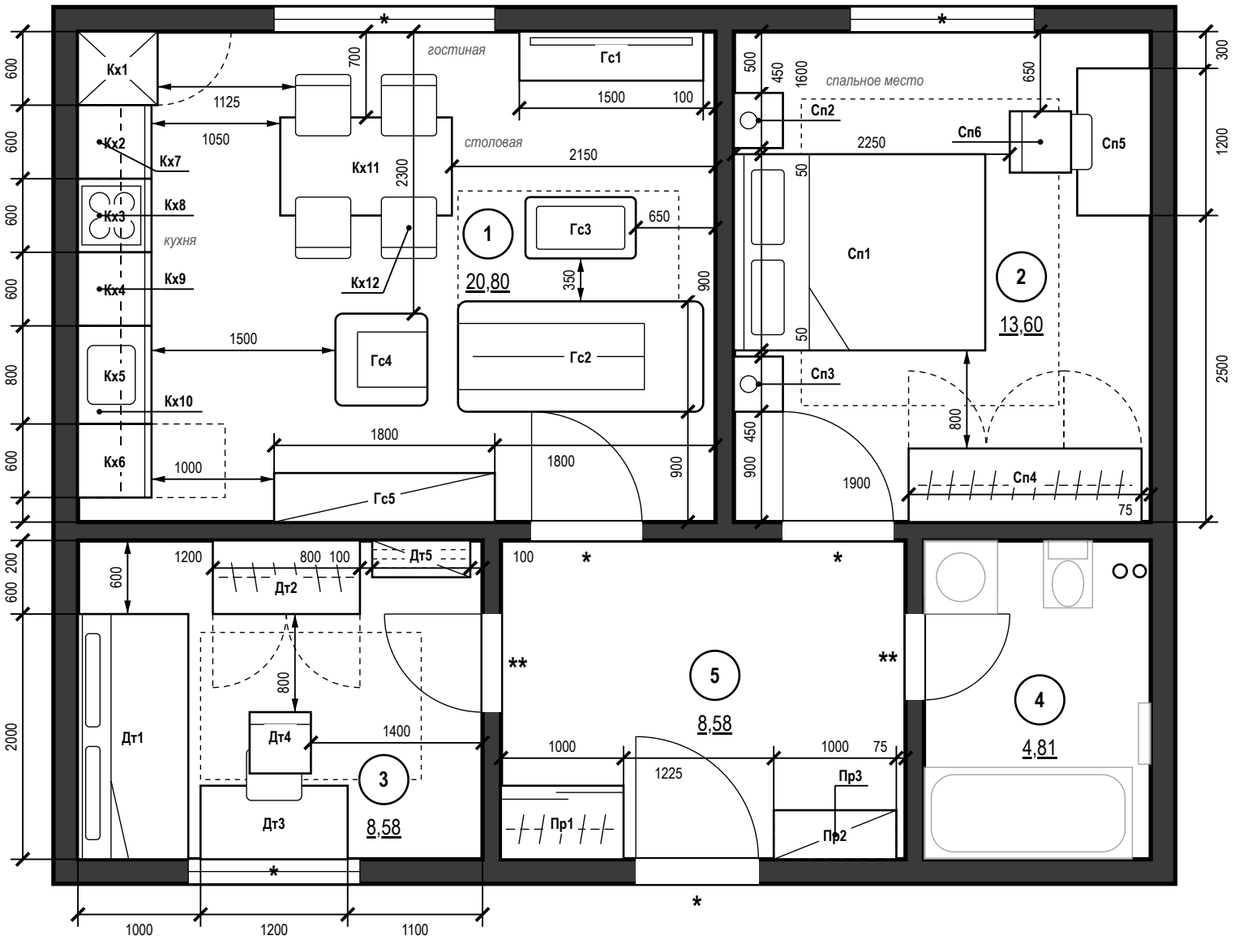

Условные обозначения

- мебель и оборудование — габарит в масштабе
- навесные шкафы (низ выше 0,9 м) — невидимый контур
- ковёр
- зона открывания дверец шкафов и техники
- **К1** — марка предмета по ведомости мебели
- привязка от чистовой стены, мм
- ширина прохода, зазор, мм
- сантехприборы — подложка (лист ВК)
- существующие стены (сечение)
- * — «*» — принято, не замерено и не подтверждено
- ** — «**» — предложение проектировщика, заказчиком не утверждено
- стояк: К1 — канализация, В1 — ХВС, Т3 — ГВС
- (1) — номер помещения, площадь м²
- *зона* — функциональная зона помещения

1000 мм · печать 1:1

Примечания

1. Размеры — в мм от чистовых поверхностей стен, привязки — от стен и углов помещения, проходы и зазоры — стрелками; розетки и выводы под мебель лист 21, выключатели — лист 23, сантехприборы — лист 31.
2. Общие указания к расстановке (чистовой слой, контрольный обмер, зазоры встроенной мебели, замена покупной) — примечания к спецификации, лист 18.
3. Отступ от стены, на плане не образмерен: Гс2 — 100 мм.
4. Стулья обеденной группы (Кх12 — 4 шт.) показаны в рабочем положении, задвинутыми под столешницу на 150 мм.

Допущения и предложения на листе

Основа листа: размеры помещений и положение проёмов введены заказчиком в брифе, на объекте не замерены (К-1); высота потолка 2700 мм — по брифу заказчика, не замерена (К-2); толщины стен приняты по брифу: наружные 200 мм, внутренние 150 мм — не обмерены (К-1); тип дома монолитный, перекрытие 200 мм — по брифу заказчика, документов нет (К-3); планировка (стены, проёмы, объединение кухни и гостиной, расширение санузла) — по брифу без обмера и плана БТИ (К-7); разрешённая мощность 10 кВт принята, ТУ не переданы (К-8); вентканалы приняты, в брифе не заданы (К-9); подрайон климата не задан — принят не северный (жилые от 2,5 м) (К-10).

Знак «*» — принято, не замерено и не подтверждено (замерить на объекте): К-1: окно пом. 1 (стена А) — окно: положение, ширина, высота и подоконник — по брифу заказчика, не замерены; ограждение 900 мм — предложение исполнителя; дверь пом. 1 (стена В) — проём в существующей стене между пом. 1 и 5: положение и ширина — по брифу заказчика, не замерены; окно пом. 2 (стена А), 3 (В) — окно: положение, ширина, высота и подоконник — по брифу заказчика, не замерены; дверь пом. 2 (стена В) — проём в существующей стене между пом. 2 и 5: положение и ширина — по брифу заказчика, не замерены; дверь пом. 5 (стена В) — входная дверь: положение и ширина проёма — по брифу заказчика, не замерены; К-4: Ст К1-1 — положение стояка канализации — по брифу заказчика, не замерено; Ст В1-1 — положение стояка холодной воды — по брифу заказчика, не замерено.

Знак «**» — предложение проектировщика, заказчиком не утверждено (согласовать с заказчиком): К-5: дверь пом. 3 (стена Б), 4 (Г) — дверь в новой перегородке: проём по брифу, короб скрытой двери и размер в свету — после выбора модели и утверждения перегородки (К-5).

Открытые вопросы и конфликты по листу: К-7.

См. лист открытых вопросов (лист 5, записи К-1–К-5, К-7–К-10).

Экспликация помещений

лист 13 · на плане — номера в марках

Ведомость мебели и оборудования

Марка	Наименование	Ш×Г×В, мм	Пом.	Кол.
Кх1	Колонна с холодильником встроенным	600×650×2350	1	1
Кх2	Модуль с ящиками	600×600×900	1	1
Кх3	Модуль с варочной панелью	600×600×900	1	1
Кх4	Модуль с ящиками	600×600×900	1	1
Кх5	Модуль под мойку	800×600×900	1	1
Кх6	Посудомоечная машина встроенная 600	600×600×900	1	1
Кх7	Навесной шкаф	600×350×900	1	1
Кх8	Вытяжка встроенная в навесной шкаф	600×350×800	1	1
Кх9	Навесной шкаф	600×350×900	1	1
Кх10	Навесной шкаф 2 секции	1400×350×900	1	1
Кх11	Стол обеденный 1400×800	1400×800×740	1	1
Гс1	Тумба ТВ низкая	1500×400×450	1	1
Гс2	Диван низкий 2000×900	900×2000×750	1	1
Гс3	Столик журнальный низкий	900×500×350	1	1
Гс4	Кресло-лаунж	750×750×750	1	1
Гс5	Консоль низкая 1800×400	1800×400×700	1	1
Сп1	Кровать-подиум 1600×2000	1600×2050×900	2	1
Сп2	Тумба прикроватная	450×400×400	2	1
Сп3	Тумба прикроватная	450×400×400	2	1
Сп4	Шкаф распашной 1900×600 до 2400	1900×600×2400	2	1
Сп5	Стол рабочий у окна 1200×600	1200×600×750	2	1
Сп6	Стул рабочий	500×500×800	2	1
Дт1	Кровать 900×2000 низкая	2000×900×700	3	1
Дт2	Шкаф 1200×600 до 2200	1200×600×2200	3	1
Дт3	Стол письменный растущий 1200×600	1200×600×700	3	1
Дт4	Стул растущий	500×500×800	3	1
Дт5	Стеллаж низкий для книг	800×300×1200	3	1
Пр1	Шкаф-купе 1000×600 до 2600	1000×600×2510	5	1
Пр2	Скамья-обувница 1000×400	1000×400×450	5	1
Пр3	Антресоль над скамьёй 1000×400	1000×400×500	5	1
Кх12	Стул обеденный к столу Кх11	450×500×820	1	4

Ш — вдоль стены (изголовья), Г — от стены (длина кровати)

Материалы, модели, допуск замены — лист 18

Изм.	Кол.уч	Лист	№ док.	Подп.	Дата
Разраб.		Кырлан А.С.			21.10.26
Пров.					
ГИП					
Н. контр.					
Утв.					

ГД-2026-011-АИ

Квартира 56 м²

ЖК «Северный парк», Москва

Дизайн-проект интерьера

Стадия	Лист	Листов
РП	17	83

План расстановки мебели

М 1:50

Кырлан Александр Сергеевич

выпуск 19.10.2026 № 1c3e34763b · стр. 21 из 117

Спецификация мебели и оборудования

ПРЕДВАРИТЕЛЬНО · не для производства работ · открыто пунктов: 10 (реестр — л. 5)

Форма 1 ГОСТ 21.110-2013 · позиции мебели — по плану расстановки

Поз.	Наименование и техническая характеристика	Тип, марка, обозначение документа, опросного листа	Код продукции	Поставщик	Ед. измерения	Кол.	Масса 1 ед., кг	Примечание
	Мебель встроенная и корпусная (изготовление по чертежам мебельщика)							
Кх1	Колонна с холодильником встроенным, фасад — дуб рифлёный; корпус ЛДСП, фасады — матовая эмаль в тон стен; Ш×Г×В 600×650×2350 мм			изготовление на заказ	шт.	1		пом. 1; крепление к стене
Кх2	Модуль с ящиками; корпус ЛДСП, фасады — матовая эмаль в тон стен; Ш×Г×В 600×600×900 мм			изготовление на заказ	шт.	1		пом. 1
Кх3	Модуль с варочной панелью и духовым шкафом; корпус ЛДСП, фасады — матовая эмаль в тон стен; Ш×Г×В 600×600×900 мм			изготовление на заказ	шт.	1		пом. 1
Кх4	Модуль с ящиками; корпус ЛДСП, фасады — матовая эмаль в тон стен; Ш×Г×В 600×600×900 мм			изготовление на заказ	шт.	1		пом. 1
Кх5	Модуль под мойку; корпус ЛДСП, фасады — матовая эмаль в тон стен; Ш×Г×В 800×600×900 мм			изготовление на заказ	шт.	1		пом. 1
Кх6	Посудомоечная машина встроенная 600; корпус ЛДСП, фасады — матовая эмаль в тон стен; Ш×Г×В 600×600×900 мм			изготовление на заказ	шт.	1		пом. 1
Кх7	Навесной шкаф, фасад — дуб рифлёный; корпус ЛДСП, фасады — матовая эмаль в тон стен; Ш×Г×В 600×350×900 мм			изготовление на заказ	шт.	1		пом. 1
Кх8	Вытяжка встроенная в навесной шкаф, рециркуляция до обмера вентканала; корпус ЛДСП, фасады — матовая эмаль в тон стен; Ш×Г×В 600×350×800 мм			изготовление на заказ	шт.	1		пом. 1
Кх9	Навесной шкаф; корпус ЛДСП, фасады — матовая эмаль в тон стен; Ш×Г×В 600×350×900 мм			изготовление на заказ	шт.	1		пом. 1
Кх10	Навесной шкаф 2 секции, с сушкой; корпус ЛДСП, фасады — матовая эмаль в тон стен; Ш×Г×В 1400×350×900 мм			изготовление на заказ	шт.	1		пом. 1
Сп4	Шкаф распашной 1900×600 до 2400, фасады — дуб рифлёный; корпус ЛДСП, фасады — матовая эмаль в цвет стен (NCS S 0804-Y30R); Ш×Г×В 1900×600×2400 мм			изготовление на заказ	шт.	1		пом. 2; крепление к стене
Дт2	Шкаф 1200×600 до 2200, фасады — дуб и серо-зелёный; корпус ЛДСП, фасады — матовая эмаль в цвет стен (NCS S 0804-Y30R); Ш×Г×В 1200×600×2200 мм			изготовление на заказ	шт.	1		пом. 3; крепление к стене
Пр1	Шкаф-купе 1000×600 до 2600, двери — дуб и зеркало; корпус ЛДСП, фасады — матовая эмаль в цвет стен (NCS S 0804-Y30R); Ш×Г×В 1000×600×2510 мм			изготовление на заказ	шт.	1		пом. 5
Пр3	Антресоль над скамьёй 1000×400, фасад в цвет стены; каркас и полки — ЛДСП, декор «дуб натуральный»; Ш×Г×В 1000×400×500 мм			изготовление на заказ	шт.	1		пом. 5; крепление к стене
	Мебель покупная							
Гс1	Тумба ТВ низкая, дуб, ТВ 55" шпон, дуб натуральный, матовое масло; Ш×Г×В 1500×400×450 мм			аналог по характеристикам	шт.	1		пом. 1; замена ≤ габарита
Гс2	Диван низкий 2000×900, лён, сиденье 400; обивка — ткань, цвет Tikkurila X447; Ш×Г×В 900×2000×750 мм			аналог по характеристикам	шт.	1		пом. 1; замена ≤ габарита
Гс3	Столик журнальный низкий, массив дуба; шпон, дуб натуральный, матовое масло; Ш×Г×В 900×500×350 мм			аналог по характеристикам	шт.	1		пом. 1; замена ≤ габарита
Гс4	Кресло-лаунж, тёмный ясень и шерсть; обивка — ткань, цвет Tikkurila X447; Ш×Г×В 750×750×750 мм			аналог по характеристикам	шт.	1		пом. 1; замена ≤ габарита
Гс5	Консоль низкая 1800×400, тёмный ясень, фасады рифлёные; шпон, дуб натуральный, матовое масло; Ш×Г×В 1800×400×700 мм			аналог по характеристикам	шт.	1		пом. 1; крепление к стене; замена ≤ габарита
Кх11	Стол обеденный 1400×800, массив дуба, низкие стулья Wishbone; шпон, дуб натуральный, матовое масло; Ш×Г×В 1400×800×740 мм			аналог по характеристикам	шт.	1		пом. 1; замена ≤ габарита
Кх12	Стул обеденный к столу Кх11; обивка — ткань, цвет Tikkurila X447; каркас — дуб натуральный; Ш×Г×В 450×500×820 мм			аналог по характеристикам	шт.	4		пом. 1; замена ≤ габарита

Примечания

1. Позиции мебели совпадают с марками на плане расстановки (лист 17); размеры Ш×Г×В — Ш вдоль стены, Г от стены.
2. Размеры и привязки плана расстановки — в мм от чистовых поверхностей стен: слой штукатурки 20 мм по блоку и 5 мм шпаклёвки по ГКЛ учтён; привязки — от стен и углов помещения, а не от другой мебели.
3. План расстановки не является документацией для изготовления мебели. Встроенная и корпусная мебель изготавливается по чертежам мебельщика после контрольного обмера (после штукатурки); «стена в стену» — с зазором 10 мм с каждой стороны или с компенсаторами; графы «Тип, марка» и «Код продукции» для неё не заполняются (ГОСТ 21.110-2013).
4. Покупные изделия — аналог по характеристикам: заменять только на изделия не больше указанного габарита и того же материала и цвета.
5. Материал и цвет, не указанные в данных изделия, приняты по концепции (лист 16): тон дерева — по полу, обивка — по вторичному цвету палитры; образцы согласовать до заказа.
6. Масса 1 ед. для изделий до 25 кг не указывается. Техника — по монтажным схемам изготовителя; выводы — по листам ЭОМ и ВК.

Допущения и предложения на листе

Основа листа: размеры помещений и положение проёмов введены заказчиком в брифе, на объекте не замерены (К-1); высота потолка 2700 мм — по брифу заказчика, не замерена (К-2); толщины стен приняты по брифу: наружные 200 мм, внутренние 150 мм — не обмерены (К-1); тип дома монолитный, перекрытие 200 мм — по брифу заказчика, документов нет (К-3); планировка (стены, проёмы, объединение кухни и гостиной, расширение санузла) — по брифу без обмера и плана БТИ (К-7); разрешённая мощность 10 кВт принята, ТУ не переданы (К-8); вентканалы приняты, в брифе не заданы (К-9); подрайон климата не задан — принят не северный (жилые от 2,5 м) (К-10).
См. лист открытых вопросов (лист 5, записи К-1–К-3, К-7–К-10).

Изм.	Кол.уч	Лист	№ док.	Подп.	Дата
Разраб.		Кырлан А.С.			21.10.26
Пров.					
ГИП					
Н. контр.					
Утв.					

ГД-2026-011-АИ

Квартира 56 м²

ЖК «Северный парк», Москва

Дизайн-проект интерьера

Стадия	Лист	Листов
РП	18	83

Спецификация мебели и оборудования

М б/м

Кырлан Александр Сергеевич

выпуск 19.10.2026 № 1c3e34763b · стр. 22 из 117

Спецификация мебели и оборудования (продолжение)

Форма 1 ГОСТ 21.110-2013 · позиции мебели — по плану расстановки

ПРЕДВАРИТЕЛЬНО · не для производства работ · открыто пунктов: 10 (реестр — л. 5)

Поз.	Наименование и техническая характеристика	Тип, марка, обозначение документа, опросного листа	Код продукции	Поставщик	Ед. измерения	Кол.	Масса 1 ед., кг	Примечание
Сп1	Кровать-подиум 1600×2000, дуб, изголовье 900; мягкое изголовье, обивка — ткань, цвет Tikkurila X447; Ш×Г×В 1600×2050×900 мм			аналог по характеристикам	шт.	1		пом. 2; замена ≤ габарита
Сп2, Сп3	Тумба прикроватная, дуб; шпон, дуб натуральный, матовое масло; Ш×Г×В 450×400×400 мм			аналог по характеристикам	шт.	2		пом. 2; замена ≤ габарита
Сп5	Стол рабочий у окна 1200×600, дуб (работа из дома); шпон, дуб натуральный, матовое масло; Ш×Г×В 1200×600×750 мм			аналог по характеристикам	шт.	1		пом. 2; замена ≤ габарита
Сп6	Стул рабочий, гнутая фанера; обивка — ткань, цвет Tikkurila X447; каркас — дуб натуральный; Ш×Г×В 500×500×800 мм			аналог по характеристикам	шт.	1		пом. 2; замена ≤ габарита
Дт1	Кровать 900×2000 низкая, дуб, спинка-бортик 700 вдоль стены; мягкое изголовье, обивка — ткань, цвет Tikkurila X447; Ш×Г×В 2000×900×700 мм			аналог по характеристикам	шт.	1		пом. 3; замена ≤ габарита
Дт3	Стол письменный растущий 1200×600; шпон, дуб натуральный, матовое масло; Ш×Г×В 1200×600×700 мм			аналог по характеристикам	шт.	1		пом. 3; замена ≤ габарита
Дт4	Стул растущий; обивка — ткань, цвет Tikkurila X447; каркас — дуб натуральный; Ш×Г×В 500×500×800 мм			аналог по характеристикам	шт.	1		пом. 3; замена ≤ габарита
Дт5	Стеллаж низкий для книг и игрушек 800×300; шпон, дуб натуральный, матовое масло; Ш×Г×В 800×300×1200 мм			аналог по характеристикам	шт.	1		пом. 3; крепление к стене; замена ≤ габарита
Пр2	Скамья-обувница 1000×400, дуб; Ш×Г×В 1000×400×450 мм			аналог по характеристикам	шт.	1		пом. 5; замена ≤ габарита
	Техника встраиваемая и бытовая, светильники под розетки							
	Холодильник встраиваемый, в модуле Кх1			аналог по характеристикам	шт.	1		пом. 1; по схеме изготовителя
	Варочная панель встраиваемая, электрическая, в модуле Кх3			аналог по характеристикам	шт.	1		пом. 1; по схеме изготовителя
	Духовой шкаф встраиваемый, в модуле Кх3			аналог по характеристикам	шт.	1		пом. 1; по схеме изготовителя
	Посудомоечная машина встраиваемая, в модуле Кх6; ниша 600 мм			аналог по характеристикам	шт.	1		пом. 1; по схеме изготовителя
	Вытяжка встраиваемая, в модуле Кх8			аналог по характеристикам	шт.	1		пом. 1; по схеме изготовителя
	Стиральная машина, место по листу ВК (Сн4); Ш×Г 600×600 мм			аналог по характеристикам	шт.	1		пом. 4; по схеме изготовителя
	Торшер, у поз. Гс2; абажур — ткань или опаловое стекло; лампа 2700 K			аналог по характеристикам	шт.	1		пом. 1; розетка Р21 (ЭОМ)
	Торшер, у поз. Сп3; абажур — ткань или опаловое стекло; лампа 2700 K			аналог по характеристикам	шт.	1		пом. 2; розетка Р5 (ЭОМ)
	Текстиль							
Т13	Портьеры-волна (гостиная); лён 70 %, вискоза 30 %; цвет Tikkurila X447; карниз 2250 мм, высота 2690 мм, сборка 2			аналог по характеристикам	шт.	2		пом. 1
Т14	Тюль (гостиная); полиэстер 100 %; цвет Tikkurila F485; карниз 2250 мм, высота 2690 мм, сборка 2,5			аналог по характеристикам	шт.	1		пом. 1
Т16	Ковёр в зоне отдыха, джут с шерстью; шерсть 100 %; цвет Tikkurila V484; 1800×1600 мм			аналог по характеристикам	шт.	1		пом. 1; с подложкой
Т17	Подушки на диван; букле (шерсть 60 %, полиэстер 40 %); цвет Tikkurila X447			аналог по характеристикам	шт.	3		пом. 1
Т18	Подушки на диван, акцент; хлопковый бархат 100 %; цвет Farrow & Ball No. 298			аналог по характеристикам	шт.	2		пом. 1

Допущения и предложения на листе

Основа листа: размеры помещений и положение проёмов введены заказчиком в брифе, на объекте не замерены (К-1); высота потолка 2700 мм — по брифу заказчика, не замерена (К-2); толщины стен приняты по брифу: наружные 200 мм, внутренние 150 мм — не обмерены (К-1); тип дома монолитный, перекрытие 200 мм — по брифу заказчика, документов нет (К-3); планировка (стены, проёмы, объединение кухни и гостиной, расширение санузла) — по брифу без обмера и плана БТИ (К-7); разрешённая мощность 10 кВт принята, ТУ не переданы (К-8); вентканалы приняты, в брифе не заданы (К-9); подрайон климата не задан — принят не северный (жилые от 2,5 м) (К-10).

См. лист открытых вопросов (лист 5, записи К-1–К-3, К-7–К-10).

Изм.	Кол.уч	Лист	№ док.	Подп.	Дата
Разраб.		Кырлан А.С.			21.10.26
Пров.					
ГИП					
Н. контр.					
Утв.					

ГД-2026-011-АИ

Квартира 56 м²

ЖК «Северный парк», Москва

Дизайн-проект интерьера

Стадия	Лист	Листов
РП	19	83

Спецификация мебели и оборудования (продолжение)

М б/м

Кырлан Александр Сергеевич

Спецификация мебели и оборудования (продолжение)

Форма 1 ГОСТ 21.110-2013 · позиции мебели — по плану расстановки

ПРЕДВАРИТЕЛЬНО · не для производства работ · открыто пунктов: 10 (реестр — л. 5)

Поз.	Наименование и техническая характеристика	Тип, марка, обозначение документа, опросного листа	Код продукции	Поставщик	Ед. измерения	Кол.	Масса 1 ед., кг	Примечание
Т19	Плед на диван; альпака 50 %, шерсть 50 %; цвет Tikkurila V484			аналог по характеристикам	шт.	1		пом. 1
Т1	Портьеры-волна; лён 100 %; цвет Tikkurila X447; карниз 2500 мм, высота 2590 мм, сборка 2			аналог по характеристикам	шт.	2		пом. 2
Т2	Тюль; полиэстер 100 %; цвет Tikkurila F485; карниз 2500 мм, высота 2590 мм, сборка 2,5			аналог по характеристикам	шт.	1		пом. 2
Т3	Ковёр под кроватью, шерсть; шерсть 80 %, хлопок 20 %; цвет NCS S 2005-Y30R; 2100×2500 мм			аналог по характеристикам	шт.	1		пом. 2; с подложкой
Т4	Подушки декоративные на кровать; лён 100 %; цвет Tikkurila X447			аналог по характеристикам	шт.	3		пом. 2
Т5	Подушки на кровать, акцент; хлопковый бархат 100 %; цвет NCS S 5010-G70Y			аналог по характеристикам	шт.	2		пом. 2
Т6	Плед на кровать; шерсть мериноса 100 %; цвет NCS S 5010-G70Y			аналог по характеристикам	шт.	1		пом. 2
Т7	Портьеры-волна; лён 100 %; цвет Tikkurila X447; карниз 1820 мм, высота 2590 мм, сборка 2			аналог по характеристикам	шт.	2		пом. 3
Т8	Тюль; полиэстер 100 %; цвет Tikkurila F485; карниз 1820 мм, высота 2590 мм, сборка 2,5			аналог по характеристикам	шт.	1		пом. 3
Т9	Ковёр игровой, шерсть; шерсть 100 %; цвет Tikkurila V484; 1800×1200 мм			аналог по характеристикам	шт.	1		пом. 3; с подложкой
Т10	Подушки декоративные на кровать; букле (шерсть 60 %, полиэстер 40 %); цвет NCS S 1002-Y50R			аналог по характеристикам	шт.	3		пом. 3
Т11	Подушки на кровать, акцент; хлопковый бархат 100 %; цвет Tikkurila X447			аналог по характеристикам	шт.	2		пом. 3
Т12	Плед на кровать; шерсть мериноса 100 %; цвет Tikkurila X447			аналог по характеристикам	шт.	1		пом. 3
	Декор							
ДК6	Картина над консолью: горный ручей, тушь суми-э, рама — тёмный ясень; 1000×700 мм; низ на 950 мм от пола			аналог по характеристикам	шт.	1	6	пом. 1; крепление: анкер, 2 шт.
ДК7	Фикус каучуконосный в кашпо Ø450, глина; 450×450 мм			аналог по характеристикам	шт.	1		пом. 1
ДК8	Ваза керамическая с одной веткой на обеденном столе; 200×350 мм; на Кх11			аналог по характеристикам	шт.	1		пом. 1
ДК1	Картина над кроватью: ветка сакуры, акварель, паспарту, рама — дуб; 1000×700 мм; низ на 1100 мм от пола			аналог по характеристикам	шт.	1	4	пом. 2; крепление к стене
ДК3	Картина над кроватью: кот на подоконнике, детская иллюстрация, рама — светлый дуб; 1200×600 мм; низ на 900 мм от пола			аналог по характеристикам	шт.	1	4	пом. 3; крепление к стене
ДК4	Зеркало в рост в тонкой чёрной раме; рама — чёрный матовый; 500×1500 мм; низ на 300 мм от пола			аналог по характеристикам	шт.	1	12	пом. 3; крепление: анкер для пустотелых оснований, 4 шт.
ДК2	Зеркало над умывальником, влагостойкое, с подсветкой; 600×800 мм; низ на 1200 мм от пола			аналог по характеристикам	шт.	1		пом. 4
ДК5	Зеркало над скамьёй, тонкая чёрная рама; рама — чёрный матовый; 600×1200 мм; низ на 700 мм от пола			аналог по характеристикам	шт.	1	18	пом. 5; крепление: анкер, 4 шт.

Допущения и предложения на листе

Основа листа: размеры помещений и положение проёмов введены заказчиком в брифе, на объекте не замерены (К-1); высота потолка 2700 мм — по брифу заказчика, не замерена (К-2); толщины стен приняты по брифу: наружные 200 мм, внутренние 150 мм — не обмерены (К-1); тип дома монолитный, перекрытие 200 мм — по брифу заказчика, документов нет (К-3); планировка (стены, проёмы, объединение кухни и гостиной, расширение санузла) — по брифу без обмера и плана БТИ (К-7); разрешённая мощность 10 кВт принята, ТУ не переданы (К-8); вентканалы приняты, в брифе не заданы (К-9); подрайон климата не задан — принят не северный (жилые от 2,5 м) (К-10).

См. лист открытых вопросов (лист 5, записи К-1–К-3, К-7–К-10).

Изм.	Кол.уч	Лист	№ док.	Подп.	Дата
Разраб.		Кырлан А.С.			21.10.26
Пров.					
ГИП					
Н. контр.					
Утв.					

ГД-2026-011-АИ

Квартира 56 м²

ЖК «Северный парк», Москва

Дизайн-проект интерьера

Стадия	Лист	Листов
РП	20	83

Спецификация мебели и оборудования (продолжение)

М б/м

Кырлан Александр Сергеевич

выпуск 19.10.2026 № 1c3e34763b · стр. 24 из 117

03

Электрооборудование


Кырлан Александр Сергеевич

выпуск 19.10.2026 · 1c3e34763b · стр. 25 из 117

План розеток и электровыводов

Розетки, выводы кабеля, щит · размеры в мм · высоты от чистого пола

ПРЕДВАРИТЕЛЬНО · не для производства работ · открыто пунктов: 10 (реестр — л. 5)

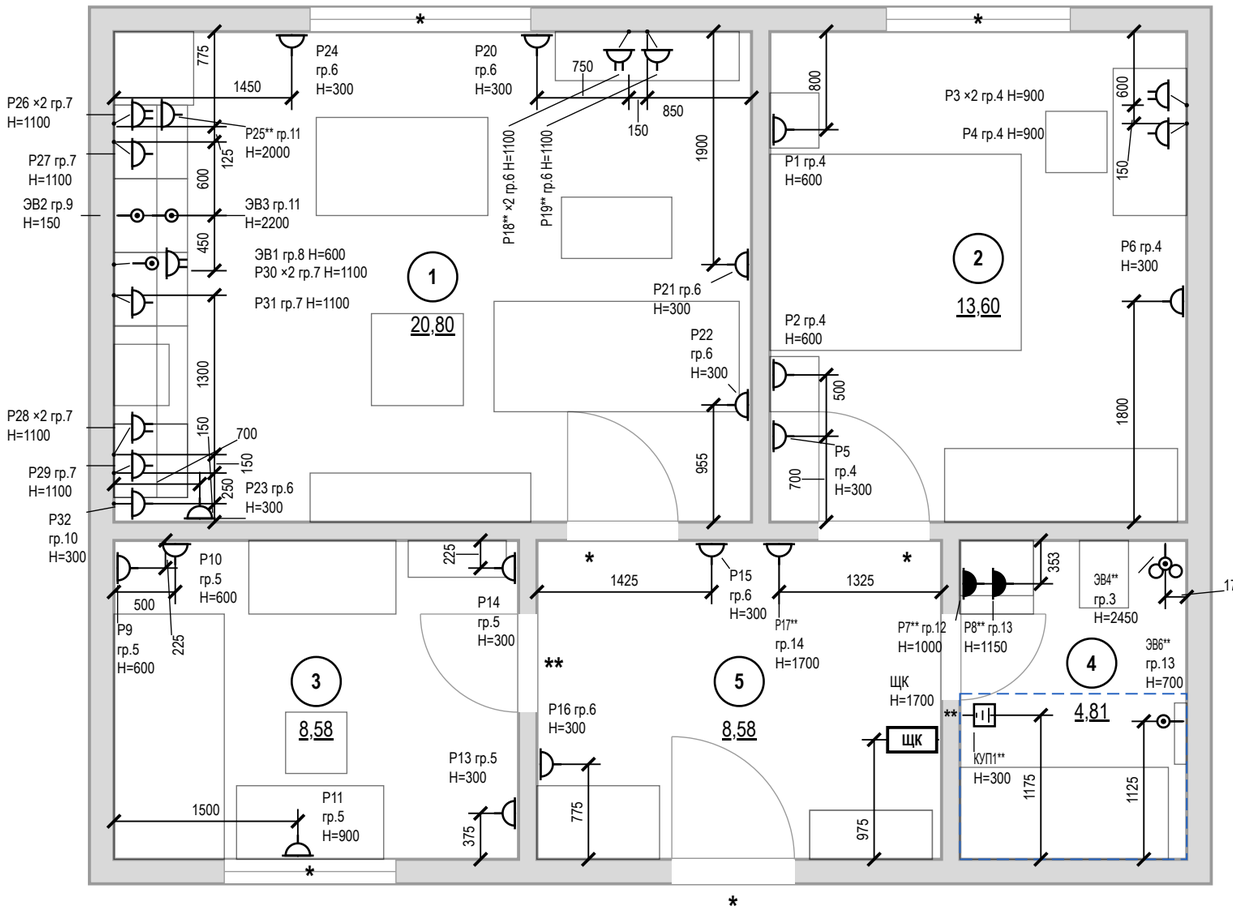

Условные обозначения

- розетка с заземляющим контактом; у знака — марка, ×N постов в рамке, гр. — группа щита, Н — высота оси, мм
- то же, рамка на 2 поста (число черточек — число постов)
- розетка влагозащищённая IP44
- вывод кабеля для подключения прибора (без розетки), марка ЭВ
- КУП — коробка уравнивания потенциалов (ДСУП), проводник к шине РЕ щита
- ЩК — щит квартирный
- знак разведён для читаемости: точка на стене — у выноски, привязка — до неё
- граница зоны 2 ванной (600 мм от ванны/поддона)
- мебель и сантехприборы — подложка
- стояк: К1 — канализация, В1 — ХВС, Т3 — ГВС
- 1 — номер помещения, площадь м²

Допущения и предложения на листе

Основа листа: размеры помещений и положение проёмов введены заказчиком в брифе, на объекте не замерены (К-1); высота потолка 2700 мм — по брифу заказчика, не замерена (К-2); толщины стен приняты по брифу: наружные 200 мм, внутренние 150 мм — не обмерены (К-1); тип дома монолитный, перекрытие 200 мм — по брифу заказчика, документов нет (К-3); планировка (стены, проёмы, объединение кухни и гостиной, расширение санузла) — по брифу без обмера и плана БТИ (К-7); разрешённая мощность 10 кВт принята, ТУ не переданы (К-8); вентканалы приняты, в брифе не заданы (К-9); подрайон климата не задан — принят не северный (жилые от 2,5 м) (К-10).

Знак «*» — принято, не замерено и не подтверждено (замерить на объекте): К-1: окно пом. 1 (стена А) — окно: положение, ширина, высота и подоконник — по брифу заказчика, не замерены; ограждение 900 мм — предложение исполнителя; дверь пом. 1 (стена В) — проём в существующей стене между пом. 1 и 5: положение и ширина — по брифу заказчика, не замерены; окно пом. 2 (стена А), 3 (В) — окно: положение, ширина, высота и подоконник — по брифу заказчика, не замерены; дверь пом. 2 (стена В) — проём в существующей стене между пом. 2 и 5: положение и ширина — по брифу заказчика, не замерены; дверь пом. 5 (стена В) — входная дверь: положение и ширина проёма — по брифу заказчика, не замерены; К-4: Ст К1-1 — положение стояка канализации — по брифу заказчика, не замерено; Ст В1-1 — положение стояка холодной воды — по брифу заказчика, не замерено.

Знак «**» — предложение проектировщика, заказчиком не утверждено (согласовать с заказчиком): К-5: дверь пом. 3 (стена Б), 4 (Г) — дверь в новой перегородке: проём по брифу, короб скрытой двери и размер в свету — после выбора модели и утверждения перегородки (К-5); записи в реестре нет: Р18 — высота 1100 мм выше нормы 1 м (ПУЭ 6.6.30) по назначению: питание ТВ, в одной зоне с выводами ТВ1 и LAN3; Р19 — высота 1100 мм выше нормы 1 м (ПУЭ 6.6.30) по назначению: питание приставки ТВ, в одной зоне с выводами ТВ1 и LAN3; Р25 — высота 2000 мм выше нормы 1 м (ПУЭ 6.6.30) по назначению: питание встроенного холодильника М6, розетка над нишей за съёмной панелью; Р7, Р8 — по образцу: Р7, Р8 и Р33 на высоте 1000 мм — верхний предел нормы (ПУЭ, п. 6.6.30, не выше 1 м); флаг решения снят; ЭВ4, КУП1 — по образцу: Добавлены выводы к вентиляторам: ЭВ4 (ВР1, ванная) и ЭВ5 (ВР3, санузел 2) — группа 3, высота 2389 мм, включение с основным светом, таймер выбега в вентиляторе; и коробки уравнивания потенциалов КУП1 (ванная) и КУП2 (санузел 2) — высота 300 мм, у входа, вне зон 0–2, проводник от шины РЕ щита ЩК, сече; ЭВ6 — по образцу: Добавлены электрические полотенцесушители IP44: П10 в ванной (480 мм, низ 900 мм) и П13 в санузле 2 (400 мм, низ 900 мм), выводы ЭВ6 и ЭВ7; мощность группы 13 — 2,4 кВт вместо 1,8 кВт; Р17 — высота 1700 мм выше нормы 1 м (ПУЭ 6.6.30) по назначению: питание слаботочного щита ЩС, рядом со щитом на его высоте.

См. лист открытых вопросов (лист 5, записи К-1–К-5, К-7–К-10).

Примечания

1. За отметку 0,000 принят уровень чистого пола. Высоты Н — от чистого пола до оси изделия; привязки — от чистовой грани стены до оси механизма (у рамки на несколько постов — до оси рамки).
2. Высота установки, не указанная на плане: розетки — 300 мм от чистого пола; выводы кабеля — по паспорту прибора.
3. Розетки в санузле — только вне зон 0–2 (ПУЭ 7.1.48, ГОСТ Р 50571.7.701-2024), IP44, через УЗО 30 мА.
4. Розеточные и мокрые линии — через УЗО или дифавтомат с током утечки не более 30 мА (ПУЭ 7.1.79); в санузле выполнить ДСУП (ПУЭ 7.1.87–7.1.88).
5. Кабель — медный, исполнение нг(А)-LS (ГОСТ 31565-2012); скрытая прокладка только горизонтально и вертикально, фактические трассы зафиксировать исполнительной схемой до закрытия отделкой.
6. Расчёт нагрузок, токов КЗ, селективности и сечений — по проекту ЭОМ организации с допуском СРО; лист задаёт состав, расположение и группы.
7. Выводы кухонной техники — после утверждения проекта кухни (ориентировочно); привязки выводов даны от осей модулей гарнитура и пересматриваются вместе с проектом кухни.
8. Электрический тёплый пол проектом не предусмотрен; при решении заказчика устроить — отдельный лист «План тёплых полов»: контуры с отступом 100 мм от стен и мебели без ножек, датчик в гофре, терморегулятор, своя группа щита через УЗО 30 мА.
9. Ведомости электроточек, изделий, светильников и расшифровка клавиш — лист 24.

1000 мм · печать 1:1

Изм.	Кол.уч	Лист	№ док.	Подп.	Дата
Разраб.		Кырлан А.С.			21.10.26
Пров.					
ГИП					
Н. контр.					
Утв.					

ГД-2026-011-АИ

Квартира 56 м²

ЖК «Северный парк», Москва

Дизайн-проект интерьера

Стадия	Лист	Листов
РП	21	83

План розеток и электровыводов


М 1:50

Кырлан Александр Сергеевич

выпуск 19.10.2026 № 1c3e34763b · стр. 26 из 117

План освещения

Светильники, группы включения, извещатели · размеры в мм

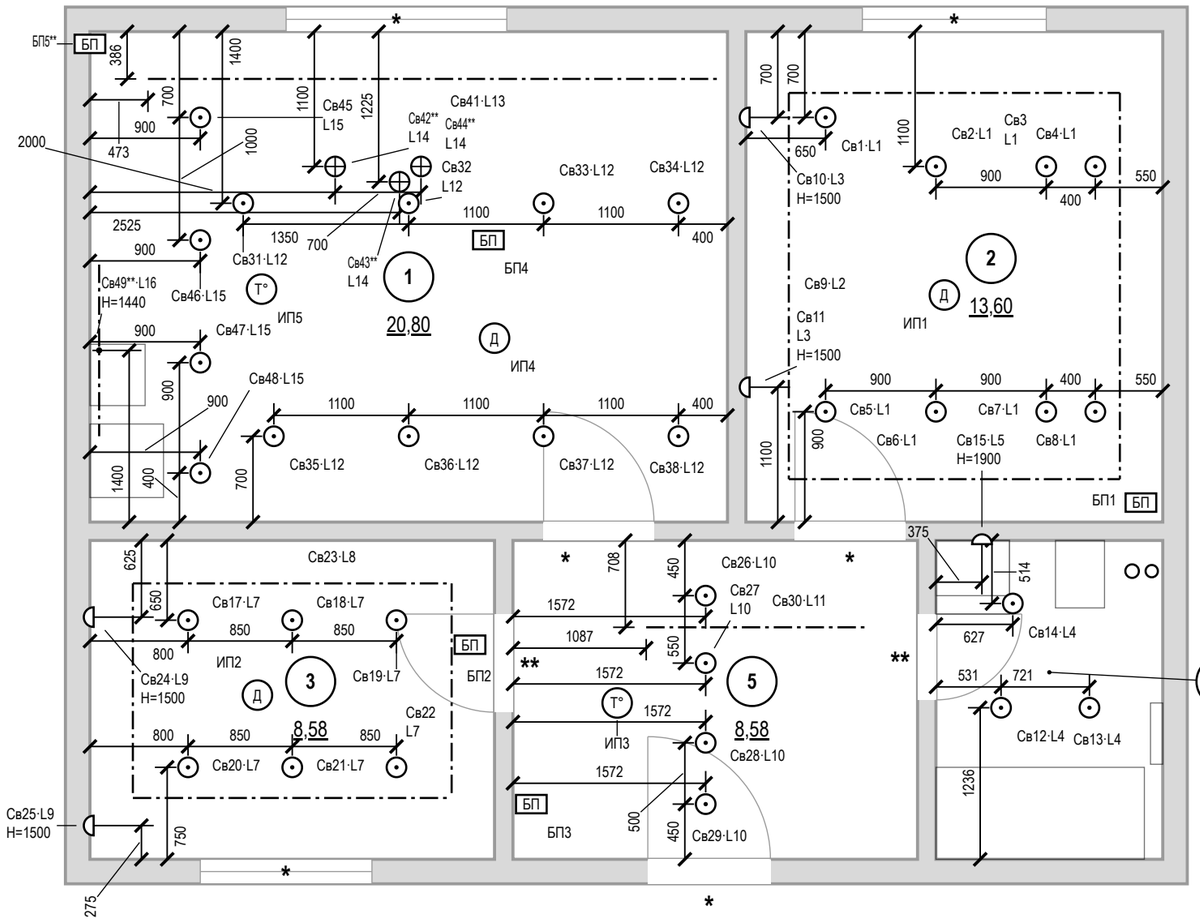

Условные обозначения

- светильник встраиваемый точечный
- светильник подвесной
- светильник настенный (бра), H — высота оси
- линейный светильник настенный (подсветка столешницы), точка — вывод питания
- светодиодная лента в профиле / в карнизе короба
- Св1·L1 — марка светильника (как в ведомости и на развёртках) · группа включения L (лист выключателей)
- Д — извещатель пожарный дымовой автономный
- T° — извещатель пожарный тепловой
- БП — блок питания LED, с доступом (люк от 100×100 мм)
- 1 — номер помещения, площадь м²

Освещённость (оценка)

Пом.	S, м²	Ен, лк	Ф треб., лм	Ф по пр., лм
1	20,8	150	8790	14000
2	13,6	150	5750	8000
3	8,6	200	4830	6300
4	4,8	50	680	1500
5	8,6	50	1210	2400

Допущения и предложения на листе

Основа листа: размеры помещений и положение проёмов введены заказчиком в брифе, на объекте не замерены (К-1); высота потолка 2700 мм — по брифу заказчика, не замерена (К-2); толщины стен приняты по брифу: наружные 200 мм, внутренние 150 мм — не обмерены (К-1); тип дома монолитный, перекрытие 200 мм — по брифу заказчика, документов нет (К-3); планировка (стены, проёмы, объединение кухни и гостиной, расширение санузла) — по брифу без обмера и плана БТИ (К-7); разрешённая мощность 10 кВт принята, ТУ не переданы (К-8); вентканалы приняты, в брифе не заданы (К-9); подрайон климата не задан — принят не северный (жилые от 2,5 м) (К-10).

Знак «*» — принято, не замерено и не подтверждено (замерить на объекте): К-1: окно пом. 1 (стена А) — окно: положение, ширина, высота и подоконник — по брифу заказчика, не замерены; ограждение 900 мм — предложение исполнителя; дверь пом. 1 (стена В) — проём в существующей стене между пом. 1 и 5: положение и ширина — по брифу заказчика, не замерены; окно пом. 2 (стена А), 3 (В) — окно: положение, ширина, высота и подоконник — по брифу заказчика, не замерены; дверь пом. 2 (стена В) — проём в существующей стене между пом. 2 и 5: положение и ширина — по брифу заказчика, не замерены; дверь пом. 5 (стена В) — входная дверь: положение и ширина проёма — по брифу заказчика, не замерены; К-4: Ст К1-1 — положение стояка канализации — по брифу заказчика, не замерено; Ст В1-1 — положение стояка холодной воды — по брифу заказчика, не замерено.

Знак «**» — предложение проектировщика, заказчиком не утверждено (согласовать с заказчиком): К-5: дверь пом. 3 (стена Б), 4 (Г) — дверь в новой перегородке: проём по брифу, короб скрытой двери и размер в свету — после выбора модели и утверждения перегородки (К-5); записи в реестре нет: Св42, Св43, Св44, Св49, БП5 — диммируемость добавлена разработчиком проекта под светорегуляторы S11 и S12.

См. лист открытых вопросов (лист 5, записи К-1–К-5, К-7–К-10).

Примечания

1. За отметку 0,000 принят уровень чистого пола. Высоты H — от чистого пола до оси изделия; привязки — от чистовой грани стены до оси механизма (у рамки на несколько постов — до оси рамки).
2. Высота установки, не указанная на плане: светильники — на потолке; настенные — по отметке H у знака. Привязки — до оси светильника от чистовой грани стены, по рядам.
3. Освещённость: Ен — СанПиН 1.2.3685-21, табл. 5.52 (на полу); Ф треб. = Ен·S·k/(U·MF) при U = 0,5 и MF = 0,71 (СП 52.13330.2016, табл. 4.3) — оценка, не светотехнический расчёт. Декоративная подсветка в Ф не входит.
4. Во влажных помещениях — светильники не ниже IP44; в зонах 0–2 ванной — по ГОСТ Р 50571.7.701-2024 (зона 1 — IPX5).
5. LED-лента в карнизе подсветки короба — по линии карниза с плана потолков; блок питания — в люке короба (БП на плане), питание ленты длиннее 5 м — с двух концов.
6. Розеточные и мокрые линии — через УЗО или дифавтомат с током утечки не более 30 мА (ПУЭ 7.1.79); в санузле выполнить ДСУП (ПУЭ 7.1.87–7.1.88).
7. Кабель — медный, исполнение нг(A)-LS (ГОСТ 31565-2012); скрытая прокладка только горизонтально и вертикально, фактические трассы зафиксировать исполнительной схемой до закрытия отделкой.
8. Расчёт нагрузок, токов КЗ, селективности и сечений — по проекту ЭОМ организации с допуском СРО; лист задаёт состав, расположение и группы.
9. Ведомость светильников — лист 24.

1000 мм · печать 1:1

Изм.	Кол.уч	Лист	№ док.	Подп.	Дата
Разраб.		Кырлан А.С.			21.10.26
Пров.					
ГИП					
Н. контр.					
Утв.					

ГД-2026-011-АИ

Квартира 56 м²

ЖК «Северный парк», Москва

Дизайн-проект интерьера

Стадия	Лист	Листов
РП	22	83

План освещения

М 1:50


Кырлан Александр Сергеевич

выпуск 19.10.2026 № 1c3e34763b · стр. 27 из 117

План выключателей и схема включения

Выключатели S, группы включения L, линии связи · размеры в мм

ПРЕДВАРИТЕЛЬНО · не для производства работ · открыто пунктов: 10 (реестр — л. 5)

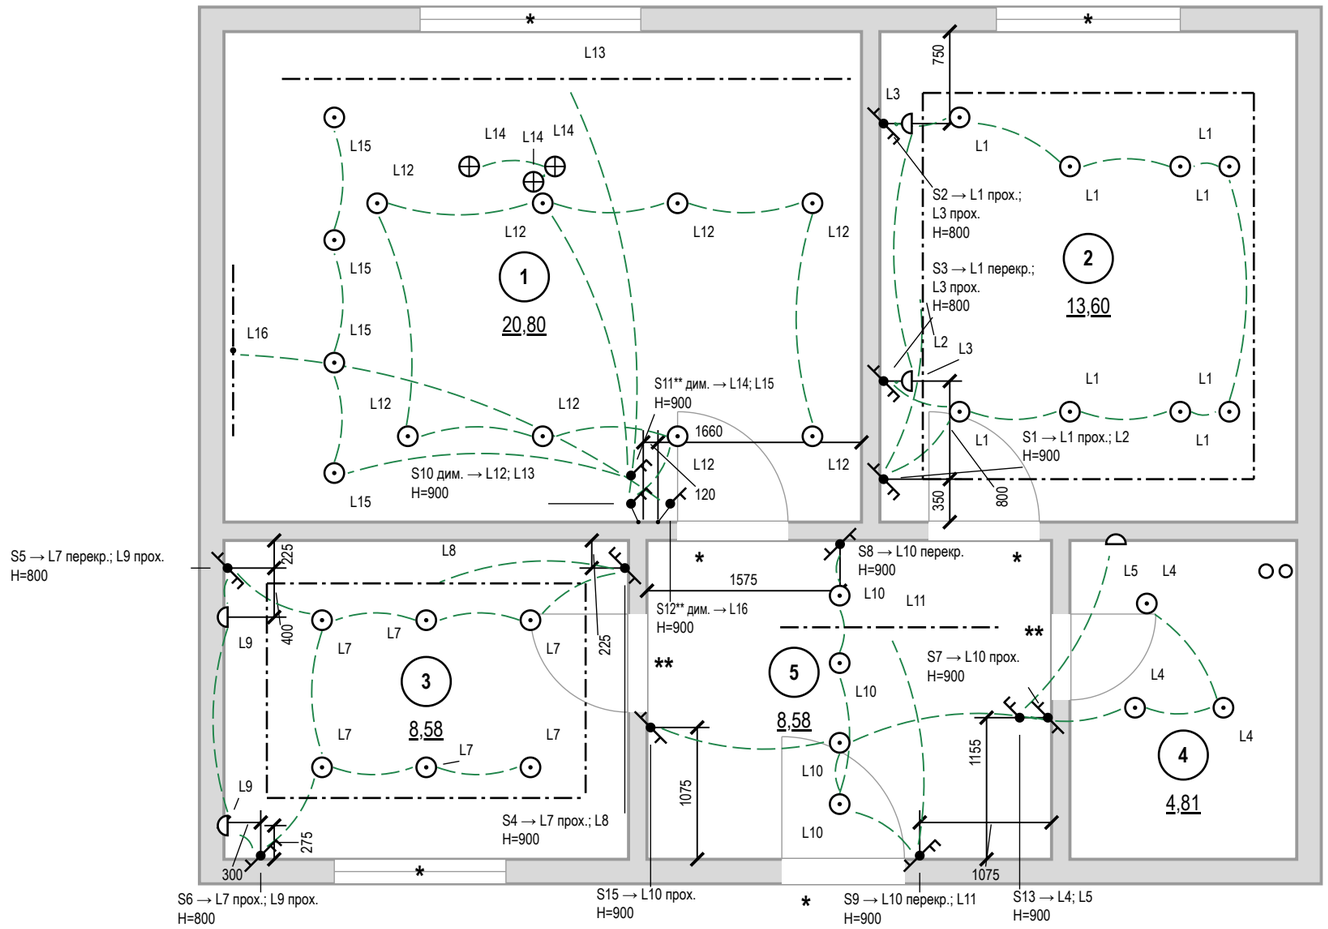

Условные обозначения

- выключатель одноклавишный
- выключатель двухклавишный (флажков — по числу клавиш)
- выключатель с проходной или перекрёстной клавишей (обратный флажок); тип клавиши — в подписи
- S1 → — марка → группы по клавишам (через «;»): прох. — проходной, перекр. — перекрёстный, дим. — светорегулятор; H — высота
- линия связи: выключатель → светильники группы (не трасса кабеля)
- светильник встраиваемый точечный
- светильник подвесной
- светильник настенный (бра), H — высота оси
- линейный светильник настенный (подсветка столешницы), точка — вывод питания
- светодиодная лента в профиле / в карнизе короба
- L1 — группа включения у светильника
- (1) — номер помещения, площадь м²

Допущения и предложения на листе

Основа листа: размеры помещений и положение проёмов введены заказчиком в брифе, на объекте не замерены (К-1); высота потолка 2700 мм — по брифу заказчика, не замерена (К-2); толщины стен приняты по брифу: наружные 200 мм, внутренние 150 мм — не обмерены (К-1); тип дома монолитный, перекрытие 200 мм — по брифу заказчика, документов нет (К-3); планировка (стены, проёмы, объединение кухни и гостиной, расширение санузла) — по брифу без обмера и плана БТИ (К-7); разрешённая мощность 10 кВт принята, ТУ не переданы (К-8); вентканалы приняты, в брифе не заданы (К-9); подрайон климата не задан — принят не северный (жилые от 2,5 м) (К-10).

Знак «*» — принято, не замерено и не подтверждено (замерить на объекте): К-1: окно пом. 1 (стена А) — окно: положение, ширина, высота и подоконник — по брифу заказчика, не замерены; ограждение 900 мм — предложение исполнителя; дверь пом. 1 (стена В) — проём в существующей стене между пом. 1 и 5: положение и ширина — по брифу заказчика, не замерены; окно пом. 2 (стена А), 3 (В) — окно: положение, ширина, высота и подоконник — по брифу заказчика, не замерены; дверь пом. 2 (стена В) — проём в существующей стене между пом. 2 и 5: положение и ширина — по брифу заказчика, не замерены; дверь пом. 5 (стена В) — входная дверь: положение и ширина проёма — по брифу заказчика, не замерены; К-4: Ст К1-1 — положение стояка канализации — по брифу заказчика, не замерено; Ст В1-1 — положение стояка холодной воды — по брифу заказчика, не замерено.

Знак «**» — предложение проектировщика, заказчиком не утверждено (согласовать с заказчиком): К-5: дверь пом. 3 (стена Б), 4 (Г) — дверь в новой перегородке: проём по брифу, короб скрытой двери и размер в свету — после выбора модели и утверждения перегородки (К-5); записи в реестре нет: S11, S12 — светорегулятор добавлен разработчиком проекта.

См. лист открытых вопросов (лист 5, записи К-1–К-5, К-7–К-10).

Примечания

1. За отметку 0,000 принят уровень чистого пола. Высоты H — от чистого пола до оси изделия; привязки — от чистовой грани стены до оси механизма (у рамки на несколько постов — до оси рамки).
2. Высота установки, не указанная на плане: выключатели — 900 мм от чистого пола, со стороны дверной ручки (ПУЭ 7.1.51).
3. Линии связи показывают, какой выключатель какую группу L включает; это не трасса кабеля. Трасса — принципиальная, фактическую зафиксировать исполнительной схемой.
4. Группы из нескольких мест (L1 — S1, S2, S3; L3 — S2, S3; L7 — S4, S5, S6; L9 — S5, S6; L10 — S7, S8, S9, S15): на крайних местах — проходные клавиши, на промежуточных — перекрёстные; механизмы — в ведомости изделий.
5. Светорегулятор — по заднему фронту (для LED-драйверов), совместимость с драйверами проверить до закупки.
6. Розеточные и мокрые линии — через УЗО или дифавтомат с током утечки не более 30 мА (ПУЭ 7.1.79); в санузле выполнить ДСУП (ПУЭ 7.1.87–7.1.88).
7. Кабель — медный, исполнение нг(А)-LS (ГОСТ 31565-2012); скрытая прокладка только горизонтально и вертикально, фактические трассы зафиксировать исполнительной схемой до закрытия отделкой.
8. Расчёт нагрузок, токов КЗ, селективности и сечений — по проекту ЭОМ организации с допуском СРО; лист задаёт состав, расположение и группы.
9. Расшифровка клавиш и ведомость изделий — лист 24.

1000 мм · печать 1:1

Изм.	Кол.уч	Лист	№ док.	Подп.	Дата
Разраб.		Кырлан А.С.			21.10.26
Пров.					
ГИП					
Н. контр.					
Утв.					

ГД-2026-011-АИ

Квартира 56 м²

ЖК «Северный парк», Москва

Дизайн-проект интерьера

Стадия	Лист	Листов
РП	23	83

План выключателей и схема включения

М 1:50

Кырлан Александр Сергеевич

выпуск 19.10.2026 № 1c3e34763b · стр. 28 из 117

Ведомость электроточек и изделий

Электроточки, изделия, светильники, клавиши выключателей · б/м

Ведомость электроточек

Марка	Пом.	Назначение	Н, мм	Гр.
Р18**	1	ТВ (в одной зоне с ТВ1, LAN3)	1100	6
Р19**	1	ТВ-приставка (в одной зоне с ТВ1, LAN3)	1100	6
Р20	1	у ТВ-тумбы	300	6
Р21	1	торшер	300	6
Р22	1	у дивана	300	6
Р23	1	уборка, пылесос	300	6
Р24	1	у обеденного стола	300	6
Р25**	1	холодильник (в навесном шкафу Кх7, съёмная панель)	2000	11
Р26	1	фартук	1100	7
Р27	1	фартук	1100	7
Р28	1	фартук	1100	7
Р29	1	фартук	1100	7
Р30	1	фартук между мойкой и варочной	1100	7
Р31	1	фартук между мойкой и варочной	1100	7
Р32	1	посудомоечная машина (на стене за торцом гарнитура, доступ сбоку)	300	10
ЭВ1	1	варочная панель (в соседнем модуле Кх4, за ящиком)	600	8
ЭВ2	1	духовой шкаф	150	9
ЭВ3	1	вытяжка	2200	11
Р1	2	у кровати	600	4
Р2	2	у кровати	600	4
Р3	2	рабочий стол	900	4
Р4	2	рабочий стол	900	4
Р5	2	торшер	300	4
Р6	2	уборка	300	4
Р9	3	у кровати	600	5
Р10	3	у кровати	600	5
Р11	3	рабочий стол	900	5
Р13	3	уборка	300	5
Р14	3	уборка у входа	300	5
КУП1**	4	КУП — уравнивание потенциалов (ДСУП)	300	

Ведомость электроточек (продолжение)

Марка	Пом.	Назначение	Н, мм	Гр.
Р7**	4	стиральная машина, IP44	1000	12
Р8**	4	фен у умывальника, IP44	1150	13
ЭВ4**	4	вентилятор ВР1 (таймер выбега)	2450	3
ЭВ6**	4	полотенцесушитель Сн5, IP44	700	13
Р15	5	пылесос, сушилка обуви	300	6
Р16	5	уборка	300	6
Р17**	5	питание слаботочного щита (рядом с ЩС**)	1700	14
ЩК	5	щит квартирный ЩРВ-П-48	1700	

Ведомость изделий

Наименование	Марки	Ед.	Кол.
Розетка с з/к и защитными шторками, 16 А	по ведомости точек	шт	34
Розетка IP44 с крышкой, 16 А	Р7**, Р8**	шт	2
Выключатель 1-клав. перекрёстный	S8	шт	1
Выключатель 1-клав. проходной	S7, S15	шт	2
Выключатель 2-клав.	S13	шт	1
Выключатель 2-клав. (перекрёстная + обычная)	S9	шт	1
Выключатель 2-клав. (перекрёстная + проходная)	S3, S5	шт	2
Выключатель 2-клав. (проходная + обычная)	S1, S4	шт	2
Выключатель 2-клав. проходной	S2, S6	шт	2
Светорегулятор 1-канальный, задний фронт (LED)	S12**	шт	1
Светорегулятор 2-канальный, задний фронт (LED)	S10, S11**	шт	2
Датчик движения ночной подсветки	L11	шт	1
Рамка 1-постовая	в т. ч. 14 под выключ.	шт	40
Рамка 2-постовая		шт	5
Коробка установочная (подрозетник) Ø68	розетки, выключатели	шт	50
Вывод кабеля под прибор (клеммник)	ЭВ1–ЭВ3, ЭВ4**, ЭВ6**	шт	5
Коробка уравнивания потенциалов КУП	КУП1**	шт	1
Блок питания LED 24 В, 300 Вт, дим.	БП4	шт	1

Ведомость изделий (продолжение)

Наименование	Марки	Ед.	Кол.
Блок питания LED 24 В, 60 Вт, дим.	БП5**	шт	1
Блок питания LED 24 В, 200 Вт, дим.	БП1, БП2	шт	2
Блок питания LED 24 В, 20 Вт	БП3	шт	1
Извещатель дымовой автономный	ИП1, ИП2, ИП4	шт	3
Извещатель тепловой	ИП3, ИП5	шт	2
Щит квартирный (состав — лист щита)	ЩК	шт	1
Розетка компьютерная RJ45, кат. 6, с рамкой и подрозетником	LAN1–LAN3	шт	3
Розетка телевизионная (коаксиальная) с рамкой и подрозетником	ТВ1	шт	1
Точка доступа Wi-Fi (оборудование заказчика), питание PoE	АР1**, АР2**	шт	2
Трубка или монитор домофона (поставка домофонной организации)	ДФ1	шт	1
Щит слаботочный ЩС**: корпус, DIN-рейка, розетки 220 В	ЩС**	шт	1
Патч-панель, портов не менее 5		шт	1
Коммутатор, портов не менее 5, из них PoE 2		шт	1
Кабель домофона — тип по системе поставщика (по лучам от ЩС**, запас 10 %)		м	6,7
Кабель коаксиальный RG-6 (75 Ом) к розеткам ТВ (по лучам от ЩС**, запас 10 %)		м	11,7
Кабель U/UTP кат. 6 (LAN, Wi-Fi и камеры по PoE) (по лучам от ЩС**, запас 10 %)		м	46,5

Ведомость светильников

Поз.	Марки	Тип	Кол.	Р, Вт	Ф, лм	IP	Тц/Ra
1	Св31–Св38	встраиваемый точечный	8	12	1000		3000/90
2	Св41	светодиодная лента, 6,4 м	1	61,4	5760		2700/90
3	Св42**, Св43**, Св44**	подвесной	3	9	800		3000/90
4	Св45–Св48	встраиваемый точечный	4	10	900		3000/90
5	Св49**	линейный светильник, Н=1440	1	18	1500		3000/90
6	Св1–Св8	встраиваемый точечный	8	12	1000		2700/90

Ведомость светильников (продолжение)

Поз.	Марки	Тип	Кол.	Р, Вт	Ф, лм	IP	Тц/Ra
7	Св9	светодиодная лента, 11,7 м	1	112,3	10530		2700/90
8	Св10, Св11, Св24, Св25	настенный (бра), Н=1500	4	6	400		2700/90
9	Св17–Св22	встраиваемый точечный	6	12	1050		2700/90
10	Св23	светодиодная лента, 8,7 м	1	83,5	7830		2700/90
11	Св12–Св14	встраиваемый точечный	3	6	500	44	3000/90
12	Св15	настенный (бра), Н=1900	1	8	600	44	3000/90
13	Св26–Св29	встраиваемый точечный	4	7	600		3000/90
14	Св30	светодиодная лента, 1,8 м	1	8,6	270		2700/90

Расшифровка клавиш

Марка	Пом.	Н, мм	Клав.	Механизм	Группа: светильники
S1	2	900	1	проходной	L1: Св1–Св8
			2	обычный	L2: Св9
S2	2	800	1	проходной	L1: Св1–Св8
			2	проходной	L3: Св10, Св11
S3	2	800	1	перекрёстный	L1: Св1–Св8
			2	проходной	L3: Св10, Св11
S4	3	900	1	проходной	L7: Св17–Св22
			2	обычный	L8: Св23
S5	3	800	1	перекрёстный	L7: Св17–Св22
			2	проходной	L9: Св24, Св25
S6	3	800	1	проходной	L7: Св17–Св22
			2	проходной	L9: Св24, Св25
S7	5	900	1	проходной	L10: Св26–Св29
S8	5	900	1	перекрёстный	L10: Св26–Св29
S9	5	900	1	перекрёстный	L10: Св26–Св29
			2	обычный	L11: Св30
S10	1	900	1	светорегулятор	L12: Св31–Св38
			2	светорегулятор	L13: Св41

Примечания

1. Ведомости сведены с планов розеток, освещения и выключателей; марки, группы и высоты — те же, что у знаков на планах.
2. Механизмы, рамки и светорегуляторы — одной серии; число постов и клавиш сверено с выбранной серией. Перекрёстная клавиша — отдельный механизм серии.
3. За отметку 0,000 принят уровень чистого пола. Высоты Н — от чистого пола до оси изделия; привязки — от чистовой грани стены до оси механизма (у рамки на несколько постов — до оси рамки).
4. Розеточные и мокрые линии — через УЗО или дифавтомат с током утечки не более 30 мА (ПУЭ 7.1.79); в санузле выполнить ДСУП (ПУЭ 7.1.87–7.1.88).
5. Кабель — медный, исполнение нг(А)-LS (ГОСТ 31565-2012); скрытая прокладка только горизонтально и вертикально, фактические трассы зафиксировать исполнительной схемой до закрытия отделкой.
6. Расчёт нагрузок, токов КЗ, селективности и сечений — по проекту ЭОМ организации с допуском СРО; лист задаёт состав, расположение и группы.
7. Ведомости занимают 2 листов этого наименования: таблицы, не вошедшие в поле листа, продолжены на следующем листе.

Допущения и предложения на листе. Знак «**» предложено (согласовать). См. лист открытых вопросов (лист 5).

Изм.	Кол.уч	Лист	№ док.	Подп.	Дата
Разраб.		Кырлан А.С.			21.10.26
Пров.					
ГИП					
Н. контр.					
Утв.					

ГД-2026-011-АИ

Квартира 56 м²

ЖК «Северный парк», Москва

Дизайн-проект интерьера

Стадия	Лист	Листов
РП	24	83

Ведомость электроточек и изделий

М б/м

Кырлан Александр Сергеевич

выпуск 19.10.2026 № 1c3e34763b · стр. 29 из 117

Ведомость электроточек и изделий (продолжение)

Электроточки, изделия, светильники, клавиши выключателей · б/м

Расшифровка клавиш (продолжение)

Марка	Пом.	Н, мм	Клав.	Механизм	Группа: светильники
S11**	1	900	1	светорегулятор	L14: Св42**, Св43**, Св44**
			2	светорегулятор	L15: Св45–Св48
S12**	1	900	1	светорегулятор	L16: Св49**
S13	5	900	1	обычный	L4: Св12–Св14
			2	обычный	L5: Св15
S15	5	900	1	проходной	L10: Св26–Св29

Допущения и предложения на листе

Основа листа: размеры помещений и положение проёмов введены заказчиком в брифе, на объекте не замерены (К-1); высота потолка 2700 мм — по брифу заказчика, не замерена (К-2); толщины стен приняты по брифу: наружные 200 мм, внутренние 150 мм — не обмерены (К-1); тип дома монолитный, перекрытие 200 мм — по брифу заказчика, документов нет (К-3); планировка (стены, проёмы, объединение кухни и гостиной, расширение санузла) — по брифу без обмера и плана БТИ (К-7); разрешённая мощность 10 кВт принята, ТУ не переданы (К-8); вентканалы приняты, в брифе не заданы (К-9); подрайон климата не задан — принят не северный (жилые от 2,5 м) (К-10).

Знак «**» — предложение проектировщика, заказчиком не утверждено (согласовать с заказчиком): записи в реестре нет: S11, S12 — светорегулятор добавлен разработчиком проекта; Св42, Св43, Св44, Св49 — диммируемость добавлена разработчиком проекта под светорегуляторы S11 и S12.

См. лист открытых вопросов (лист 5, записи К-1–К-3, К-7–К-10).

Примечания

1. Продолжение ведомостей: лист 2 из 2 этого наименования; таблицы, прерванные на предыдущем листе, продолжены с заголовком «(продолжение)».
2. За отметку 0,000 принят уровень чистого пола. Высоты Н — от чистого пола до оси изделия; привязки — от чистовой грани стены до оси механизма (у рамки на несколько постов — до оси рамки).
3. Розеточные и мокрые линии — через УЗО или дифавтомат с током утечки не более 30 мА (ПУЭ 7.1.79); в санузле выполнить ДСУП (ПУЭ 7.1.87–7.1.88).
4. Кабель — медный, исполнение нг(А)-LS (ГОСТ 31565-2012); скрытая прокладка только горизонтально и вертикально, фактические трассы зафиксировать исполнительной схемой до закрытия отделкой.
5. Расчёт нагрузок, токов КЗ, селективности и сечений — по проекту ЭОМ организации с допуском СРО; лист задаёт состав, расположение и группы.

Изм.	Кол.уч	Лист	№ док.	Подп.	Дата
Разраб.		Кырлан А.С.			21.10.26
Пров.					
ГИП					
Н. контр.					
Утв.					

ГД-2026-011-АИ

Квартира 56 м²

ЖК «Северный парк», Москва

Дизайн-проект интерьера

Стадия	Лист	Листов
РП	25	83

Ведомость электроточек и изделий (продолжение)


М б/м

Кырлан Александр Сергеевич

выпуск 19.10.2026 № 1c3e34763b · стр. 30 из 117

Однолинейная схема щита

Щит квартирный ЩК · без масштаба

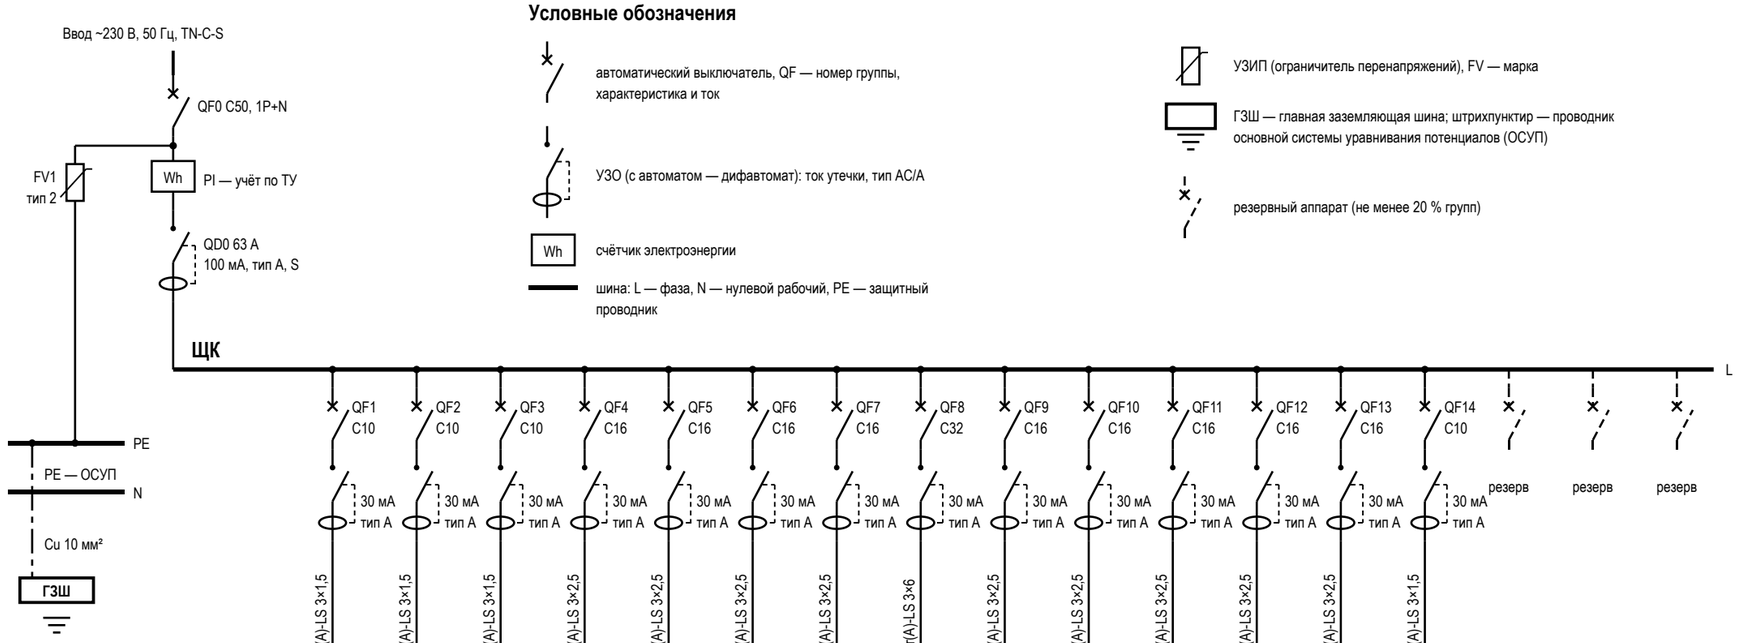

Условные обозначения

- автоматический выключатель, QF — номер группы, характеристика и ток
- УЗО (с автоматом — дифавтомат): ток утечки, тип AC/A
- Wh — счётчик электроэнергии
- шина: L — фаза, N — нулевой рабочий, PE — защитный проводник
- УЗИП (ограничитель перенапряжений), FV — марка
- ГЗШ — главная заземляющая шина; штрихпунктир — проводник основной системы уравнивания потенциалов (ОСУП)
- резервный аппарат (не менее 20 % групп)

Данные щитка

Показатель	Значение
Номер щитка	ЩК
Тип	ЩРВ-П-48, IP41
Уст. мощность, кВт	24,6
Разреш. мощность, кВт	10
Расчётная, кВт	9,6
Автоматы 1п: занят. / рез.	14 / 3
Модулей: всего / занято	48 / 34
Ток на вводе, А	50
Вводной аппарат	QF0 C50, 1P+N
УЗИП	FV1, тип 2, ЩК, после счётчика
ГЗШ, проводник ОСУП	Cu 10 мм²

Таблица групп щита ЩК и кабельный журнал

№	Назначение	Помещения	Автомат	УЗО / дифавтомат	Кабель	Длина, м	P, кВт	Точек
1	освещение спальни и детской	2, 3	C10	30 мА, тип A	ВВГнг(A)-LS 3×1,5	75	0,4	28
2	освещение гостиной-кухни и прихожей	1, 5	C10	30 мА, тип A	ВВГнг(A)-LS 3×1,5	77	0,5	32
3	освещение и вентилятор санузла	4, 5	C10	30 мА, тип A	ВВГнг(A)-LS 3×1,5	16	0,1	6
4	розетки спальни	2	C16	30 мА, тип A	ВВГнг(A)-LS 3×2,5	25	1,5	6
5	розетки детской	3	C16	30 мА, тип A	ВВГнг(A)-LS 3×2,5	24	1,5	5
6	розетки гостиной и прихожей	1, 5	C16	30 мА, тип A	ВВГнг(A)-LS 3×2,5	45	2	9
7	розетки фартука кухни	1	C16	30 мА, тип A	ВВГнг(A)-LS 3×2,5	30	2,5	6
8	варочная панель	1	C32	30 мА, тип A	ВВГнг(A)-LS 3×6	17	7	1
9	духовой шкаф	1	C16	30 мА, тип A	ВВГнг(A)-LS 3×2,5	17	3	1
10	посудомоечная машина	1	C16	30 мА, тип A	ВВГнг(A)-LS 3×2,5	16	2	1
11	холодильник и вытяжка	1	C16	30 мА, тип A	ВВГнг(A)-LS 3×2,5	16	0,6	2
12	стиральная машина	4	C16	30 мА, тип A	ВВГнг(A)-LS 3×2,5	8	2,2	1
13	розетки санузла (фен), полотенцесушитель	4	C16	30 мА, тип A	ВВГнг(A)-LS 3×2,5	14	1,2	2
14	слаботочный щит (роутер, ONT)	5	C10	30 мА, тип A	ВВГнг(A)-LS 3×1,5	6	0,1	1
	Итого по сечениям ВВГнг(A)-LS, м: 3×1,5 — 174; 3×2,5 — 195; 3×6 — 17					386		

Допущения и предложения на листе

Основа листа: размеры помещений и положение проёмов введены заказчиком в брифе, на объекте не замерены (К-1); высота потолка 2700 мм — по брифу заказчика, не замерена (К-2); толщины стен приняты по брифу: наружные 200 мм, внутренние 150 мм — не обмерены (К-1); тип дома монолитный, перекрытие 200 мм — по брифу заказчика, документов нет (К-3); планировка (стены, проёмы, объединение кухни и гостиной, расширение санузла) — по брифу без обмера и плана БТИ (К-7); разрешённая мощность 10 кВт принята, ТУ не переданы (К-8); вентканалы приняты, в брифе не заданы (К-9); подрайон климата не задан — принят не северный (жилые от 2,5 м) (К-10).

Открытые вопросы и конфликты по листу: К-8.

См. лист открытых вопросов (лист 5, записи К-1–К-3, К-7–К-10).

Примечания

1. Схема однолинейная: одна линия — фаза, N и PE группы; аппараты — в отключённом положении (ГОСТ 2.702, ГОСТ 2.755). Номера групп — как у точек на планах (гр.). За отметку 0,000 принят уровень чистого пола; высота щита — по плану розеток.
2. Розеточные и мокрые линии — через УЗО или дифавтомат с током утечки не более 30 мА (ПУЭ 7.1.79); в санузле выполнить ДСУП (ПУЭ 7.1.87–7.1.88).
3. УЗО тип A — для линий с электроникой, стиральной и посудомоечной машиной, LED-драйверами; тип AC — только для чисто активной нагрузки.
4. Кабель — медный, исполнение нг(A)-LS (ГОСТ 31565-2012); скрытая прокладка только горизонтально и вертикально, фактические трассы зафиксировать исполнительной схемой до закрытия отделкой.
5. Номинал автомата — не выше допустимого тока кабеля: 1,5 мм² — до 10 А, 2,5 мм² — до 16 А. Резерв щита — не менее 20 % модулей.
6. Расчёт нагрузок, токов КЗ, селективности и сечений — по проекту ЭОМ организации с допуском СРО; лист задаёт состав, расположение и группы.
7. УЗИП FV1 — после вводного автомата, проводник к шине PE — кратчайший, без петель. Шина PE щита соединяется с ГЗШ проводником ОСУП; к ГЗШ присоединяются трубы водопровода и отопления на вводе в квартиру (ПУЭ 7.1.87). Шины N и PE — раздельные, после разделения PEN не объединяются.
8. До подключения нагрузки — приёмо-сдаточные испытания с протоколом: сопротивление изоляции линий не менее 0,5 МОм, срабатывание УЗО по току и времени, непрерывность защитных проводников PE (ПУЭ, гл. 1.8).

Изм.	Кол.уч	Лист	№ док.	Подп.	Дата
Разраб.		Кырлан А.С.			21.10.26
Пров.					
ГИП					
Н. контр.					
Утв.					

ГД-2026-011-АИ

Квартира 56 м²

ЖК «Северный парк», Москва

Дизайн-проект интерьера

Стадия	Лист	Листов
РП	26	83

Однолинейная схема щита

М б/м


Кырлан Александр Сергеевич

План принципиальных трасс

Силовые трассы и объёмы электромонтажа, слаботочка в объёмах · размеры в мм

ПРЕДВАРИТЕЛЬНО · не для производства работ · открыто пунктов: 10 (реестр — л. 5)

Допущения и предложения на листе. Основа листа: размеры помещений и положение проёмов введены заказчиком в брифе, на объекте не замерены (К-1); высота потолка 2700 мм — по брифу заказчика, не замерена (К-2); толщины стен приняты по брифу: наружные 200 мм, внутренние 150 мм — не обмерены (К-1); тип дома монолитный, перекрытие 200 мм — по брифу заказчика, документов нет (К-3); планировка (стены, проёмы, объединение кухни и гостиной, расширение санузла) — по брифу без обмера и плана БТИ (К-7); разрешённая мощность 10 кВт принята, ТУ не переданы (К-8); вентканалы приняты, в брифе не заданы (К-9); подрайон климата не задан — принят не северный (жилые от 2,5 м) (К-10). Знак «*» — принято, не замерено и не подтверждено (замерить на объекте): К-4: Ст К1-1 — положение стояка канализации — по брифу заказчика, не замерено; Ст В1-1 — положение стояка холодной воды — по брифу заказчика, не замерено. Знак «**» — предложение проектировщика, заказчиком не утверждено (согласовать с заказчиком): записи в реестре нет: ЩС — щит слаботочный: место и состав. См. лист открытых вопросов (лист 5, записи К-1–К-5, К-7–К-10).

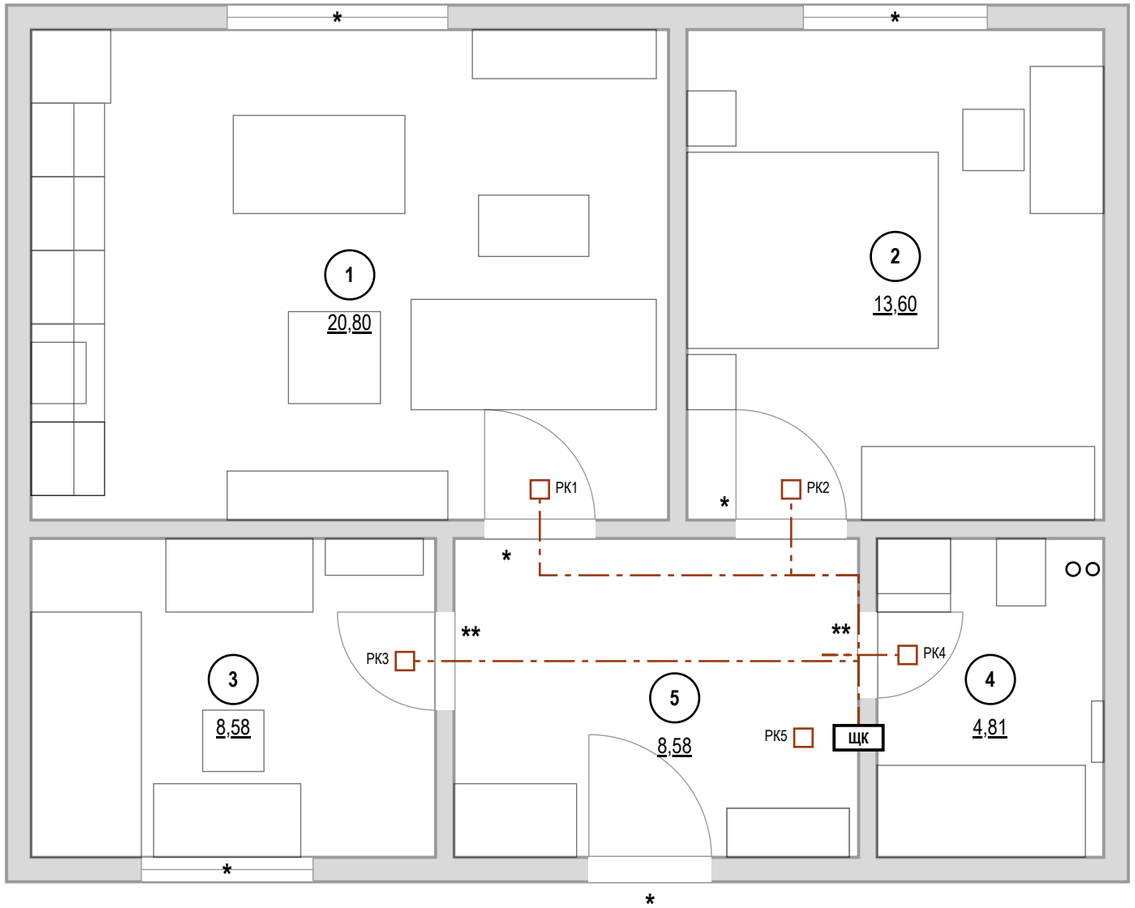

Кабель по группам ВВГнг(А)-LS, м

Гр.	мм²	Трасса	Данные
1	3×1,5	73,9	75
2	3×1,5	78,1	77
3	3×1,5	15,7	16
4	3×2,5	24,9	25
5	3×2,5	23,7	24
6	3×2,5	43,2	45
7	3×2,5	29,6	30

Гр.	мм²	Трасса	Данные
8	3×6	16,5	17
9	3×2,5	16,5	17
10	3×2,5	14	16
11	3×2,5	15,9	16
12	3×2,5	7,5	8
13	3×2,5	13,6	14
14	3×1,5	5,4	6
Σ		**378,5**	**386**

Экспликация помещений

№	Помещение	Площадь, м²
1	Гостиная-кухня	20,80
2	Спальня	13,60
3	Детская	8,58
4	Санузел	4,81
5	Прихожая	8,58
	Итого (общая площадь)	56,37

Объёмы прокладки

Работа, материал	Ед.	Кол.
Гофротруба Ø20 в потолочном пространстве	м	129,7
Кабель-канал плинтуса для силовых линий	м	101,5
Короб или накладной канал для вертикальных спусков и подъёмов	м	75,7
Коробка распределительная (РК) над дверью помещения	шт	5
Слаботочка: кабель домофона	м	6,7
Слаботочка: Кабель коаксиальный RG-6 (75 Ом) к розеткам ТВ	м	11,7
Слаботочка: U/UTP кат. 6 (LAN, Wi-Fi, камеры)	м	46,5
Слаботочка: гофротруба Ø20 отдельно от силовых	м	58,4

Штробы — только после заключения

Работа	Ед.	Кол.
Вертикальные штробы 20×20 мм от потолка до каждой настенной точки (в маршрут без штроб не входят)	м	94,01

Условные обозначения

- **ЩК** — щит квартирный
- РК — распределительная коробка над дверью помещения
- магистраль от щита к РК: потолочное пространство, гофра
- мебель и сантехприборы — подложка

Примечания

1. За отметку 0,000 принят уровень чистого пола. Высоты Н — от чистого пола до оси изделия; привязки — от чистовой грани стены до оси механизма (у рамки на несколько постов — до оси рамки).
2. Розеточные и мокрые линии — через УЗО или дифавтомат с током утечки не более 30 мА (ПУЭ 7.1.79); в санузле выполнить ДСУП (ПУЭ 7.1.87–7.1.88).
3. Кабель — медный, исполнение нг(А)-LS (ГОСТ 31565-2012); скрытая прокладка только горизонтально и вертикально, фактические трассы зафиксировать исполнительной схемой до закрытия отделкой.
4. Расчёт нагрузок, токов КЗ, селективности и сечений — по проекту ЭОМ организации с допуском СРО; лист задаёт состав, расположение и группы.
5. Длины — по плану: от щита вверх в потолочное пространство, по дверям и коридору без захода в мокрые помещения к распределительной коробке над дверью, далее к точкам; вертикали считаются вниз и обратно (у последней точки цепочки — в один конец); запас 10 %. Трассы принципиальные: фактическую зафиксировать исполнительной схемой до закрытия отделкой.
6. Несущие стены не определены: штробы в стенах не выполнять. Маршрут проложен без штроб: горизонтали — за потолком в гофре (129,7 м) и в кабель-канале плинтуса (101,5 м), вертикали — в коробе или накладном канале (133,3 м кабеля). Точек: за потолком — 43, спуск из потолка — 12, по плинтусу — 13, плинтус и подъём 33.
7. Вариант со штробами — работа после технического заключения: 94,01 м вертикальных штроб от потолка до каждой настенной точки; условие — только после технического заключения: стена не несущая (или вертикальная штроба в несущей согласована конструктором), глубина и ширина 20–25 мм, не в зонах 0–2 ванной. Без заключения и согласования конструктора в смету и в график эта работа не входит.
8. В данных проекта (журнал щита) длины кабеля внесены оценкой (386 м), по трассам из геометрии — 379 м (-2 %): к закупке и в смету принимать длины по трассам, а оценку в данных проекта заменить.
9. Слаботочные сети: кабели и точки считаются по лучам от ЩС** (лист слаботочных сетей): 65 м, портов патч-панели и коммутатора не менее 5; из точек 2 предложения листа слаботочки, не подтверждённые заказчиком. Изделия — в ведомости изделий.

1000 мм · печать 1:1

Изм.	Кол.уч	Лист	№ док.	Подп.	Дата
Разраб.		Кырлан А.С.			21.10.26
Пров.					
ГИП					
Н. контр.					
Утв.					

ГД-2026-011-АИ

Квартира 56 м²

ЖК «Северный парк», Москва

Дизайн-проект интерьера

Стадия	Лист	Листов
РП	27	83

План принципиальных трасс

М 1:50


Кырлан Александр Сергеевич

выпуск 19.10.2026 № 1c3e34763b · стр. 32 из 117

План слаботочных сетей

Интернет, ТВ, домофон · размеры в мм · высоты от чистого пола

ПРЕДВАРИТЕЛЬНО · не для производства работ · открыто пунктов: 10 (реестр — л. 5)

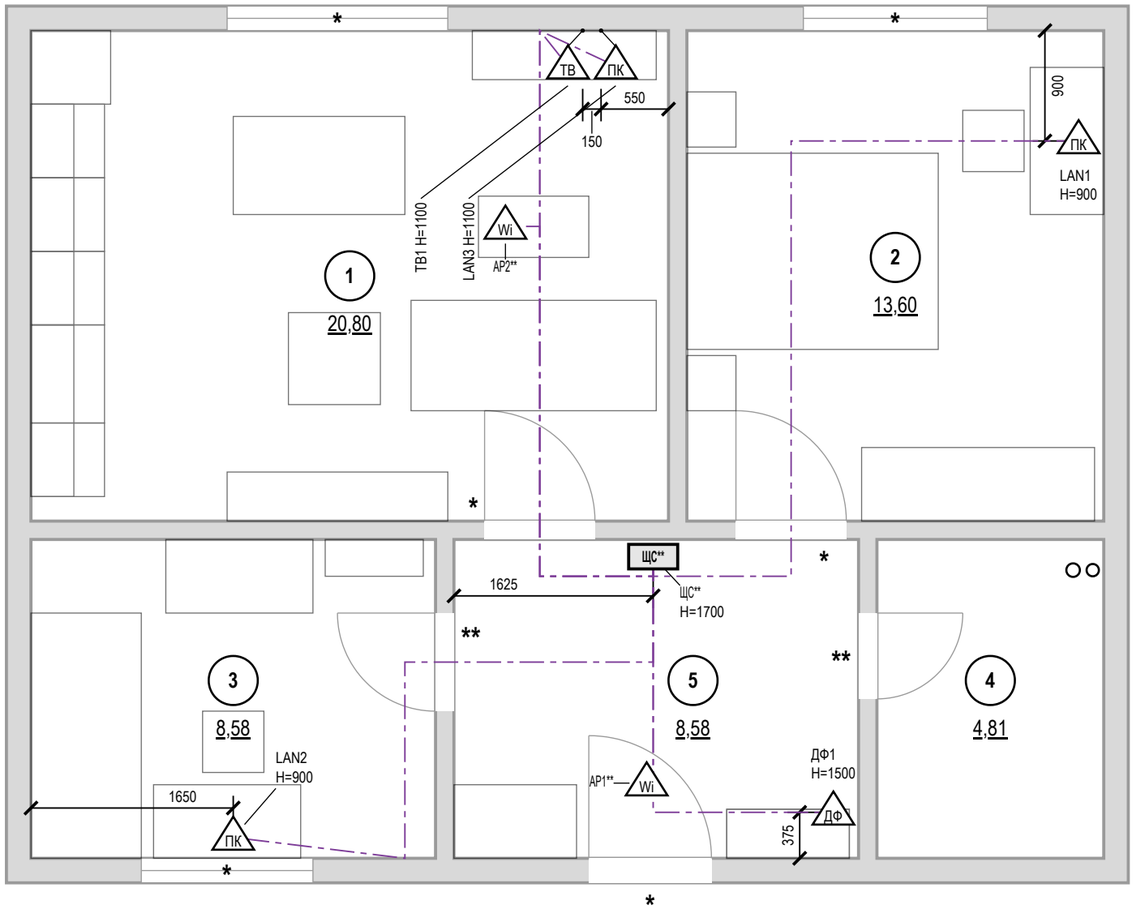

Ведомость слаботочных точек

Марка	Пом.	Назначение	H, мм	Кабель
TB1	1	розетка ТВ	1100	RG-6
LAN3	1	розетка LAN (RJ45)	1100	U/UTP кат. 6
AP2**	1	точка доступа Wi-Fi		U/UTP кат. 6
LAN1	2	розетка LAN (RJ45)	900	U/UTP кат. 6
LAN2	3	розетка LAN (RJ45)	900	U/UTP кат. 6
ЩС**	5	щит слаботочный	1700	ввод пров.
ДФ1	5	домофон (трубка)	1500	по системе
AP1**	5	точка доступа Wi-Fi		U/UTP кат. 6

Условные обозначения

- **ЩС** — щит слаботочный: ввод провайдера, роутер, коммутатор
- ПК — розетка компьютерная RJ45
- ТВ — розетка телевизионная
- ДФ — трубка или монитор домофона
- Wi — точка доступа Wi-Fi (питание PoE)
- кабель от ЩС до точки, отдельным лучом
- мебель и сантехприборы — подложка
- (1) — номер помещения, площадь м²

Допущения и предложения на листе

Основа листа: размеры помещений и положение проёмов введены заказчиком в брифе, на объекте не замерены (К-1); высота потолка 2700 мм — по брифу заказчика, не замерена (К-2); толщины стен приняты по брифу: наружные 200 мм, внутренние 150 мм — не обмерены (К-1); тип дома монолитный, перекрытие 200 мм — по брифу заказчика, документов нет (К-3); планировка (стены, проёмы, объединение кухни и гостиной, расширение санузла) — по брифу без обмера и плана БТИ (К-7); разрешённая мощность 10 кВт принята, ТУ не переданы (К-8); вентканалы приняты, в брифе не заданы (К-9); подрайон климата не задан — принят не северный (жилые от 2,5 м) (К-10).

Знак «*» — принято, не замерено и не подтверждено (замерить на объекте): К-1: окно пом. 1 (стена А) — окно: положение, ширина, высота и подоконник — по брифу заказчика, не замерены; ограждение 900 мм — предложение исполнителя; дверь пом. 1 (стена В) — проём в существующей стене между пом. 1 и 5: положение и ширина — по брифу заказчика, не замерены; окно пом. 2 (стена А), 3 (В) — окно: положение, ширина, высота и подоконник — по брифу заказчика, не замерены; дверь пом. 2 (стена В) — проём в существующей стене между пом. 2 и 5: положение и ширина — по брифу заказчика, не замерены; дверь пом. 5 (стена В) — входная дверь: положение и ширина проёма — по брифу заказчика, не замерены; К-4: Ст К1-1 — положение стояка канализации — по брифу заказчика, не замерено; Ст В1-1 — положение стояка холодной воды — по брифу заказчика, не замерено.

Знак «**» — предложение проектировщика, заказчиком не утверждено (согласовать с заказчиком): К-5: дверь пом. 3 (стена Б), 4 (Г) — дверь в новой перегородке: проём по брифу, короб скрытой двери и размер в свету — после выбора модели и утверждения перегородки (К-5); записи в реестре нет: AP2, AP1 — точка доступа Wi-Fi: число и места; ЩС — щит слаботочный: место и состав.

См. лист открытых вопросов (лист 5, записи К-1–К-5, К-7–К-10).

Примечания

1. За отметку 0,000 принят уровень чистого пола. Высоты H — от чистого пола до оси изделия; привязки — от чистовой грани стены до оси механизма (у рамки на несколько постов — до оси рамки).
2. Высота установки, не указанная на плане: розетки LAN и ТВ — 300 мм от чистого пола.
3. Слаботочные кабели — отдельно от силовых: в своей трубе или лотке, при параллельной прокладке не ближе 100 мм к силовым, пересечения под прямым углом; каждую точку — отдельным кабелем от ЩС** без скруток.
4. Трассы на листе — принципиальные; фактические зафиксировать исполнительной схемой до закрытия отделкой. Силовые линии, УЗО 30 мА, ДСУП, кабель нг(А)-LS — по листам розеток и щита.
5. Проект силовой части и расчёт токов КЗ — по проекту ЭОМ; слаботочная часть согласуется с провайдером и управляющей компанией (домофон, коллективное ТВ).

1000 мм · печать 1:1

Изм.	Кол.уч	Лист	№ док.	Подп.	Дата
Разраб.		Кырлан А.С.			21.10.26
Пров.					
ГИП					
Н. контр.					
Утв.					

ГД-2026-011-АИ

Квартира 56 м²

ЖК «Северный парк», Москва

Дизайн-проект интерьера

Стадия	Лист	Листов
РП	28	83

План слаботочных сетей

М 1:50

Кырлан Александр Сергеевич

выпуск 19.10.2026 № 1c3e34763b · стр. 33 из 117

04

Отопление и вентиляция


Кырлан Александр Сергеевич

выпуск 19.10.2026 · 1c3e34763b · стр. 34 из 117

План вентиляции

Вытяжка, приток, переток · кондиционирование не предусмотрено · размеры в мм · высоты от чистого пола

ПРЕДВАРИТЕЛЬНО · не для производства работ · открыто пунктов: 10 (реестр — л. 5)

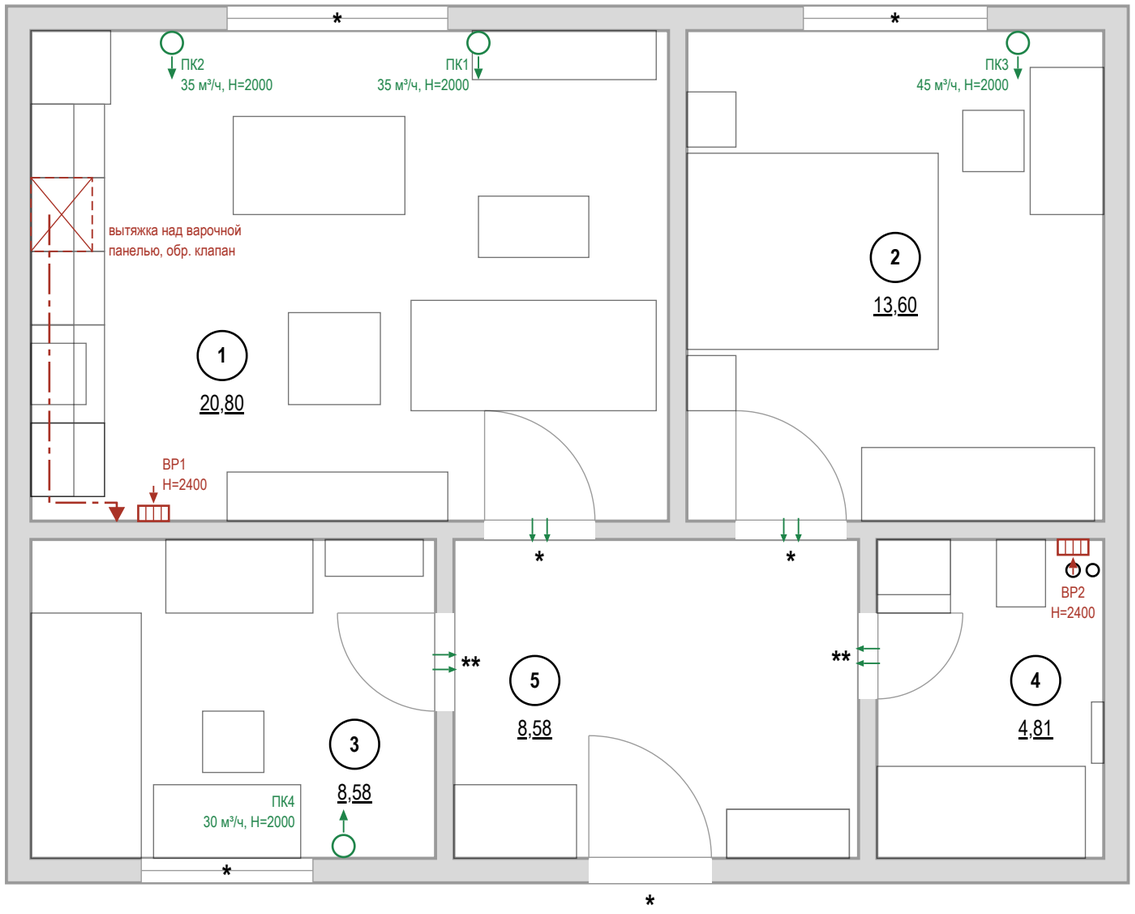

Условные обозначения

- стояк: К1 — канализация, В1 — ХВС, Т3 — ГВС
- 1 — номер помещения, площадь м²
- вытяжная решётка в вентканал: марка, расход м³/ч, H центра от чистого пола
- приточный клапан (КИВ) в наружной стене: марка, расход, H центра
- переток: зазор под полотном или переточная решётка
- кухонная вытяжка над варочной панелью
- воздуховод кухонной вытяжки в коробе под потолком
- отдельный вход воздуховода в вентканал, обратный клапан
- * — «*» — принято, не замерено и не подтверждено
- ** — «**» — предложение проектировщика, заказчиком не утверждено

Воздухообмен, м³/ч

№	Помещение	Выт. норма	Выт. проект	Прит. норма	Прит. проект	Устройства
1	Гостиная-кухня	60	60	63	70	ВР1, ПК1, ПК2
2	Спальня			41	45	ПК3
3	Детская			26	30	ПК4
4	Санузел	50	**25 !**			ВР2
	Итого	**110**	**85**	**130**	**145**	

Воздухообмен квартиры — по большей из сумм притока и вытяжки: норма 130 м³/ч, проект 145 м³/ч.
Приток больше вытяжки на 60 м³/ч — поднять вытяжку.
«!» — проект ниже нормы.

Допущения и предложения на листе. Основа листа: размеры помещений и положение проёмов введены заказчиком в брифе, на объекте не замерены (К-1); высота потолка 2700 мм — по брифу заказчика, не замерена (К-2); толщины стен приняты по брифу: наружные 200 мм, внутренние 150 мм — не обмерены (К-1); тип дома монолитный, перекрытие 200 мм — по брифу заказчика, документов нет (К-3); планировка (стены, проёмы, объединение кухни и гостиной, расширение санузла) — по брифу без обмера и плана БТИ (К-7); разрешённая мощность 10 кВт принята, ТУ не переданы (К-8); вентканалы приняты, в брифе не заданы (К-9); подрайон климата не задан — принят не северный (жилые от 2,5 м) (К-10). Знак «*» — принято, не замерено и не подтверждено (замерить на объекте): К-4: Ст К1-1 — положение стояка канализации — по брифу заказчика, не замерено; Ст В1-1 — положение стояка холодной воды — по брифу заказчика, не замерено. Знак «**» — предложение проектировщика, заказчиком не утверждено (согласовать с заказчиком). См. лист открытых вопросов (лист 5, записи К-1–К-5, К-7–К-10); по листу — К-9.

Примечания

1. Расчёт систем ОВ и подбор оборудования — проектная организация с допуском СРО; лист даёт места, трассы и привязки.
2. Нормы вытяжки — СП 54.13330.2022 (Изм. 1, 2), табл. 7.1: кухня с электроплитой 60 м³/ч, с газовой 100; ванная и совмещённый санузел 50; уборная 25; гардеробная 0,2 ч⁻¹. Приток в жилые — 3 м³/ч на 1 м² (менее 20 м² общей площади на человека), иначе 30 м³/ч на человека.
3. Вентканалы и шахты не сужать, не переносить и не закрывать; вентилятор и кухонная вытяжка — через обратный клапан, без перекрытия естественной тяги.
4. Проектные расходы — не ниже нормы, вытяжка сведена с притоком вентиляторами мокрых помещений. Клапаны — в простенке у окна, центр 2000 мм, не над кроватью, не ближе 300 мм к стоякам отопления; типоразмер — на расход.
5. Кухонная вытяжка в воздухообмен не включена: воздуховод не менее Ø125 в коробе, вход в канал отдельный.
6. Переток — зазор под полотнами межкомнатных дверей или переточная решётка.
7. Кондиционирование заданием не предусмотрено; при установке трассы фреона и дренажа (не менее 40 мм/м, в К1 через сифон) и питание заложить до черновых работ.
8. Привязки оборудования — по паспортам приобретённых моделей, до черновых работ.
9. Знак «*» у проёма — допущение: положение проёма не замерено (окно пом. 1, стена А; дверь пом. 1, стена В; окно пом. 2, стена А; дверь пом. 2, стена В; окно пом. 3, стена В; дверь пом. 5, стена В); размер напечатан как принятый. Реестр: лист 5, вопрос К-1.
10. Клапаны ПК1, ПК2, ПК3, ПК4 выведены в простенок у окна, положение которого — допущение (знак «*»): после обмера окна привязку сверить.

1000 мм · печать 1:1

Изм.	Кол.уч	Лист	№ док.	Подп.	Дата
Разраб.		Кырлан А.С.			21.10.26
Пров.					
ГИП					
Н. контр.					
Утв.					

ГД-2026-011-АИ

Квартира 56 м²

ЖК «Северный парк», Москва

Дизайн-проект интерьера

Стадия	Лист	Листов
РП	29	83

План вентиляции


М 1:50

Кырлан Александр Сергеевич

выпуск 19.10.2026 № 1c3e347763b · стр. 35 из 117

План отопления

Радиаторы, стояки, подводки · размеры в мм · высоты от чистого пола

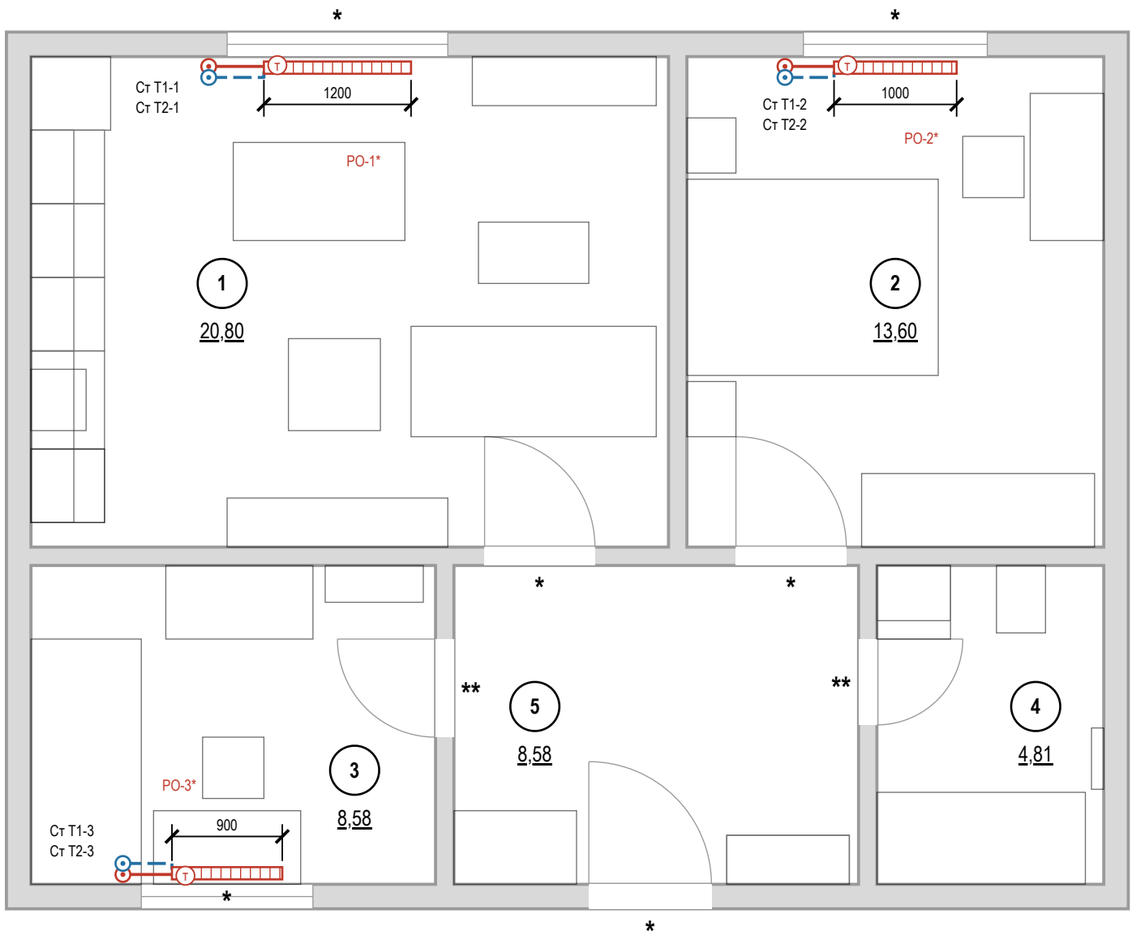

Примечания

1. Расчёт системы отопления, теплопотерь и подбор приборов — проектная организация с допуском СРО; лист даёт места и привязки.
2. Тип, длина и мощность радиаторов — по теплотехническому расчёту; лист задаёт места, зазоры и подключение.
3. Радиаторы — под каждым окном жилых комнат и кухни, центр по оси проёма, длина 0,7 ширины окна (кратно 100); окончательно — по расчёту.
4. Зазоры радиатора: низ не менее 100 мм от чистого пола, верх не менее 100 мм до подоконника, 30–50 мм от стены до задней панели; центр по оси окна с допуском ±20 мм.
5. Радиаторы не закрывать глухими коробами и мебелью; перенос и замена приборов в многоквартирном доме — переустройство, согласование с управляющей организацией (ЖК РФ ст. 25–26); вынос на лоджию запрещён.
6. Трубы отопления через межквартирные стены не прокладывать (СП 51.13330.2011, п. 9.19); через перекрытия и перегородки — в гильзах.
7. Привязки приборов и подводок — по паспортам приобретённых радиаторов и клапанов, до черновых работ.
8. До закрытия отделкой трубопроводы отопления испытать гидростатическим давлением с оформлением акта (СП 73.13330.2016, 7.2–7.3).
9. Знак «*» у проёма — допущение: положение проёма не замерено (окно пом. 1, стена А; дверь пом. 1, стена В; окно пом. 2, стена А; дверь пом. 2, стена В; окно пом. 3, стена В; дверь пом. 5, стена В); размер напечатан как принятый. Реестр: лист 5, вопрос К-1.
10. Радиаторы РО-1, РО-2, РО-3 стоят по оси окна, положение которого — допущение (знак «*»): после обмера окна привязки приборов и подводок сверить.

Допущения и предложения на листе. Основа листа: размеры помещений и положение проёмов введены заказчиком в брифе, на объекте не замерены (К-1); высота потолка 2700 мм — по брифу заказчика, не замерена (К-2); толщины стен приняты по брифу: наружные 200 мм, внутренние 150 мм — не обмерены (К-1); тип дома монолитный, перекрытие 200 мм — по брифу заказчика, документов нет (К-3); планировка (стены, проёмы, объединение кухни и гостиной, расширение санузла) — по брифу без обмера и плана БТИ (К-7); разрешённая мощность 10 кВт принята, ТУ не переданы (К-8); вентканалы приняты, в брифе не заданы (К-9); подрайон климата не задан — принят не северный (жилые от 2,5 м) (К-10). Знак «*» — принято, не замерено и не подтверждено (замерить на объекте). Знак «**» — предложение проектировщика, заказчиком не утверждено (согласовать с заказчиком). См. лист открытых вопросов (лист 5, записи К-1–К-3, К-5, К-7–К-10).

1000 мм · печать 1:1

ПРЕДВАРИТЕЛЬНО · не для производства работ · открыто пунктов: 10 (реестр — л. 5)

Условные обозначения

- 1 — номер помещения, площадь м²
- радиатор отопления (марка РО-N, длина по плану)
- клапан с термоголовкой на подаче
- стояк отопления, подающий (Ст Т1-N)
- стояк отопления, обратный (Ст Т2-N)
- Т1 — отопление, подающий трубопровод
- Т2 — отопление, обратный трубопровод
- * — «*» — принято, не замерено и не подтверждено
- ** — «**» — предложение проектировщика, заказчиком не утверждено

Ведомость радиаторов

Марка	Помещение	Тип	Д×В×Г, мм	Низ / стена	Q, Вт
РО-1	1. Гостиная-кухня	панельный*	1200×600×100	120 / 40	расч.
РО-2	2. Спальня	панельный*	1000×600×100	120 / 40	расч.
РО-3	3. Детская	панельный*	900×600×100	120 / 40	расч.

* тип и мощность — по теплотехническому расчёту
Низ — от чистого пола, стена — зазор до задней панели, мм.

Привязки — до обмера
Стояки отопления в исходных данных не заданы: показаны у откосов окон, подводки — принципиально. До черновых работ — обмер стояков и паспорта приборов; лист перевыпустить по факту.

Изм.	Кол.уч	Лист	№ док.	Подп.	Дата
Разраб.		Кырлан А.С.			21.10.26
Пров.					
ГИП					
Н. контр.					
Утв.					

ГД-2026-011-АИ

Квартира 56 м²

ЖК «Северный парк», Москва

Дизайн-проект интерьера

Стадия	Лист	Листов
РП	30	83

План отопления

М 1:50

Кырлан Александр Сергеевич

выпуск 19.10.2026 № 1c3e34763b · стр. 36 из 117

05

Водоснабжение и канализация

Кырлан Александр Сергеевич


выпуск 19.10.2026 · 1c3e34763b · стр. 37 из 117

План выводов сантехники


Выводы В1, Т3, К1 · привязки от чистовых стен · высоты от чистого пола, мм

ПРЕДВАРИТЕЛЬНО · не для производства работ · открыто пунктов: 10 (реестр — л. 5)

Фрагмент 1. Гостиная-кухня (пом. 1)

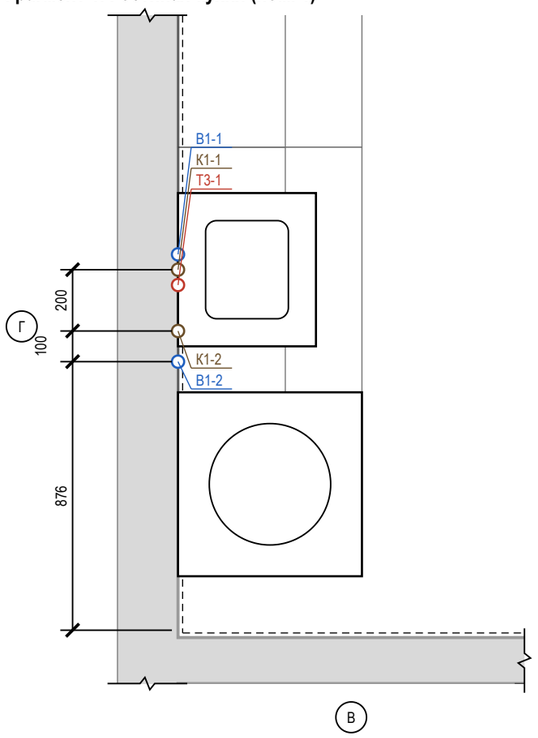

Фрагмент 2. Санузел (пом. 4)

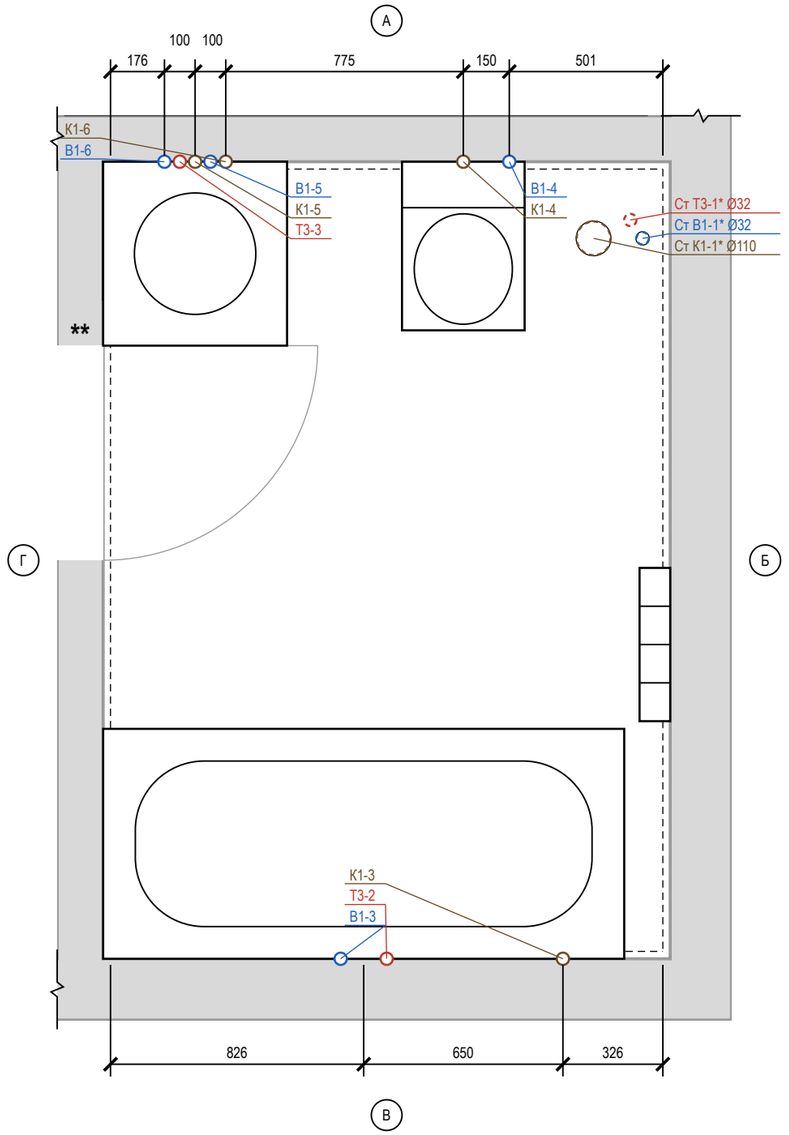

Ведомость привязок выводов

Код	Прибор	Ø	H, мм	Привязка от чист. стен, мм	Прим.
В1-1	П1 мойка кухонная	½"	600*	ст. Г: 1226 от В	межос. 100
Т3-1	П1 мойка кухонная	½"	600*	ст. Г: 1126 от В	межос. 100
К1-1	П1 мойка кухонная	Ø50	400*	ст. Г: 1176 от В	
В1-2	П2 посудомоечная машина	½"	550*	ст. Г: 876 от В	кран ПММ в шкафу мойки
К1-2	П2 посудомоечная машина	Ø40	550*	ст. Г: 976 от В	слив ПММ в шкафу мойки
В1-3	Сн1 ванна	½"	800*	ст. В: 751 от Г	межос. 150
Т3-2	Сн1 ванна	½"	800*	ст. В: 901 от Г	межос. 150
К1-3	Сн1 ванна	Ø50	50*	ст. В: 326 от Б	
В1-4	Сн2 унитаз подвесной	½"	250*	ст. А: 501 от Б	в раме инсталляции
К1-4	Сн2 унитаз подвесной	Ø110	220*	ст. А: 651 от Б	
В1-5	Сн3 умывальник	½"	600*	ст. А: 326 от Г	межос. 100
Т3-3	Сн3 умывальник	½"	600*	ст. А: 226 от Г	межос. 100
К1-5	Сн3 умывальник	Ø50	500*	ст. А: 276 от Г	
В1-6	Сн4 стиральная машина	½"	600*	ст. А: 176 от Г	кран машины
К1-6	Сн4 стиральная машина	Ø50	600*	ст. А: 376 от Г	

* — высота по практике монтажа; сверить по паспорту прибора

Условные обозначения

- вывод В1 (код — в ведомости привязок)
- вывод Т3 (код — в ведомости привязок)
- вывод К1 (код — в ведомости привязок)
- сантехприбор по расстановке (габарит модели)
- чистовая поверхность стены (от неё привязки)
- стояк «Ст К1-N / Ст В1-N» (ГОСТ 21.601), Ø мм
- * стояк Т3 не на обмере — принят в шахте рядом со Ст В1, сверить
- * у стояка — положение принято, не замерено, сверить
- линия обрыва (граница фрагмента)
- А обозначение стены А–Г (как на развёртках)

Допущения и предложения на листе

Основа листа: размеры помещений и положение проёмов введены заказчиком в брифе, на объекте не замерены (К-1); высота потолка 2700 мм — по брифу заказчика, не замерена (К-2); толщины стен приняты по брифу: наружные 200 мм, внутренние 150 мм — не обмерены (К-1); тип дома монолитный, перекрытие 200 мм — по брифу заказчика, документов нет (К-3); планировка (стены, проёмы, объединение кухни и гостиной, расширение санузла) — по брифу без обмера и плана БТИ (К-7); разрешённая мощность 10 кВт принята, ТУ не переданы (К-8); вентканалы приняты, в брифе не заданы (К-9); подрайон климата не задан — принят не северный (жилые от 2,5 м) (К-10).

Знак «*» — принято, не замерено и не подтверждено (замерить на объекте): К-4: Ст К1-1 — положение стояка канализации — по брифу заказчика, не замерено; Ст В1-1 — положение стояка холодной воды — по брифу заказчика, не замерено.

Знак «**» — предложение проектировщика, заказчиком не утверждено (согласовать с заказчиком): К-5: дверь пом. 4 (стена Г) — дверь в новой перегородке: проём по брифу, короб скрытой двери и размер в свету — после выбора модели и утверждения перегородки (К-5).

Открытые вопросы и конфликты по листу: К-4, К-9.

См. лист открытых вопросов (лист 5, записи К-1–К-5, К-7–К-10).

Примечания

1. Привязки выводов даны от чистовых поверхностей стен (облицовка на сторону: гостиная-кухня — 24 мм (фартук: штукатурка 10 + клей 5 + плитка 9); санузел — 24 мм (штукатурка 10 + клей 5 + плитка 9)); эти же грани — на развёртках и в раскладке плитки. Высоты — от чистого пола помещения.
2. Высоты и межосевые, отмеченные «*», приняты по практике монтажа; до черновой разводки сверить по паспорту выбранного прибора (смеситель, инсталляция, сифон).
3. Горячая вода (Т3) — слева от холодной (В1), если смотреть на прибор. Допуск установки выводов: ±5 мм в группе, ±20 мм у отдельно стоящих.
4. Расчёт систем водоснабжения и канализации и подбор оборудования выполняет проектная организация; лист задаёт места и высоты выводов.
5. Посудомоечная машина П2: кран и слив — отдельными выводами в шкафу мойки (не за машиной), до машины ≤ 1500 мм.
6. Ст К1-1*, Ст В1-1*, Ст Т3-1 на обмере не показаны: приняты рядом с Ст В1-1* (в МКД стоят группой); положение сверить на объекте до разметки.
7. Стояки в коробах/шахтах не замоноличивать; стояк К1 в коробе — звукоизоляция стояка в коробе без жёсткого контакта с трубой; к арматуре и ревизиям — люк не меньше 300×400.
8. Знак «*» у стояка — положение принято, не замерено (все стояки); сверить на объекте до разметки. Реестр: лист 5, вопрос К-4.

1000 мм · печать 1:1

Изм.	Кол.уч	Лист	№ док.	Подп.	Дата
Разраб.		Кырлан А.С.			21.10.26
Пров.					
ГИП					
Н. контр.					
Утв.					

ГД-2026-011-АИ

Квартира 56 м²

ЖК «Северный парк», Москва

Дизайн-проект интерьера

Стадия	Лист	Листов
РП	31	83

План выводов сантехники

М 1:20

Кырлан Александр Сергеевич


выпуск 19.10.2026 № 1c3e34763b · стр. 38 из 117

Схема разводки водопровода и канализации


Схемы систем В1, Т3, К1 · трассы принципиальные · уклоны в мм на 1 м · план М 1:200, фрагменты М 1:25

ПРЕДВАРИТЕЛЬНО · не для производства работ · открыто пунктов: 10 (реестр — л. 5)


План квартиры (М 1:200)

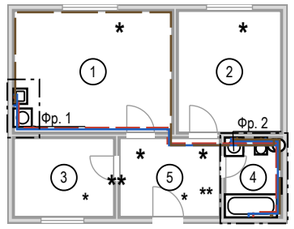

Фр. 1. Гостиная-кухня (М 1:25)

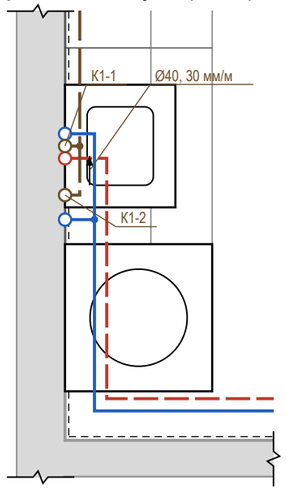

Фр. 2. Санузел (М 1:25)

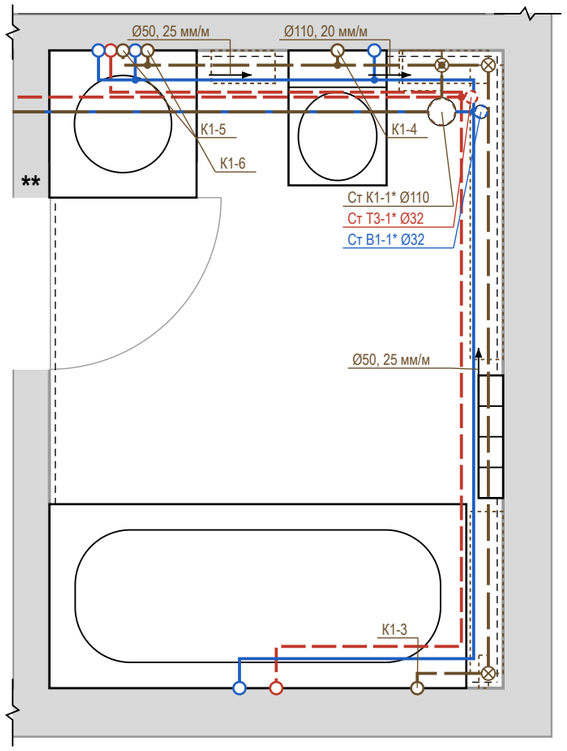

Условные обозначения

- В1 — водопровод хозяйственно-питьевой (ХВС), PP-R Ø20
- Т3 — горячее водоснабжение, подача (ГВС), PP-R Ø20
- К1 — канализация бытовая
- направление уклона К1 / пола: Ø, мм на 1 м
- ревизия (прочистка) К1 — доступ сохранить
- тройник (ответвление к прибору)
- короб К1 над чистым полом (ГКЛВ под плитку)
- вывод В1 (код — в ведомости привязок)
- вывод Т3 (код — в ведомости привязок)
- вывод К1 (код — в ведомости привязок)
- сантехприбор по расстановке (габарит модели)
- стояк «Ст К1-N / Ст В1-N» (ГОСТ 21.601), Ø мм
- * стояк Т3 не на обмере — принят в шахте рядом со Ст В1, сверить
- * у стояка — положение принято, не замерено, сверить
- линия обрыва (граница фрагмента)
- граница фрагмента на плане (Фр. N)

Профиль выпусков К1 (до врезки в стояк)

Выпуск	Прибор	Ø	L, м	i, мм/м	Δh, мм	Прокладка, мм
К1-4	Сн2 унитаз подвесной	Ø110	0,68	20	14	короб 160×140
К1-1	П1 мойка кухонная	Ø50	15,58	25	390	короб 470×110
К1-3	Сн1 ванна	Ø50	3,21	25	80	короб 160×110
К1-5	Сн3 умывальник	Ø50	1,55	25	39	короб 120×110
К1-6	Сн4 стиральная машина	Ø50	1,45	25	36	короб 120×110
К1-2	П2 посудомоечная машина	Ø40	15,78	30	473	короб 550×110

Короб h×b: h — от чистого пола, b — от чистовой стены. Стяжка 35 мм — лист полов.

Узел ввода В1, Т3 (схема, без масштаба)



⊗ Ст К1-1*: ревизия на стояке — люк в коробе

Допущения и предложения на листе. Основа листа: размеры помещений и положение проёмов введены заказчиком в брифе, на объекте не замерены (К-1); высота потолка 2700 мм — по брифу заказчика, не замерена (К-2); толщины стен приняты по брифу: наружные 200 мм, внутренние 150 мм — не обмерены (К-1); тип дома монолитный, перекрытие 200 мм — по брифу заказчика, документов нет (К-3); планировка (стены, проёмы, объединение кухни и гостиной, расширение санузла) — по брифу без обмера и плана БТИ (К-7); разрешённая мощность 10 кВт принята, ТУ не переданы (К-8); вентканалы приняты, в брифе не заданы (К-9); подрайон климата не задан — принят не северный (жилые от 2,5 м) (К-10). Знак «*» — принято, не замерено и не подтверждено (замерить на объекте): К-4: Ст К1-1 — положение стояка канализации — по брифу заказчика, не замерено; Ст В1-1 — положение стояка холодной воды — по брифу заказчика, не замерено. Знак «**» — предложение проектировщика, заказчиком не утверждено (согласовать с заказчиком). См. лист открытых вопросов (лист 5, записи К-1–К-5, К-7–К-10); по листу — К-4.

Примечания

1. Трассы принципиальные, построены от стояков вдоль стен помещений; фактическое положение фиксируется исполнительной схемой с привязками (фото с рулеткой) до закрытия.
2. Уклон К1 не менее 1/d и не более 150 мм/м (СП 30.13330.2020, п. 19.1), приняты практические уклоны; поворот — двумя отводами 45°, ревизия после поворота, доступ сохранить. Стояк К1 в коробе — звукоизоляция стояка в коробе, без жёсткого контакта короба с трубой.
3. Решение по К1: стяжка 35 мм не укрывает трубы (нужно Ø + Δh + 45 мм) — выпуски идут над чистым полом вдоль стен; К1-4, К1-1, К1-3, К1-5, К1-6, К1-2 — в коробе ГКЛВ под плитку (размеры в профиле). Короба — на развёртках; отметку низа врезки в стояк замерить до черновых работ.
4. На каждом вводе В1 и Т3 — кран шаровой, фильтр, счётчик, обратный клапан; доступ через люк не меньше 300×400. Водопровод — в штробе стен или в коробах; трубы испытать давлением до закрытия (акт скрытых работ).
5. Расчёт систем, диаметры магистралей и подбор оборудования выполняет проектная организация; врезка и перенос стояков — по согласованию с управляющей организацией. Арматуру и привязки сверить по паспортам приборов.
6. Ст К1-1*, Ст В1-1*, Ст Т3-1 на обмере не показаны: приняты рядом с Ст В1-1*; положение сверить на объекте до разводки.
7. Знак «*» у стояка — положение принято, не замерено (все стояки); сверить на объекте до разметки. Реестр: лист 5, вопрос К-4.

Изм.	Кол.уч	Лист	№ док.	Подп.	Дата
Разраб.		Кырлан А.С.			21.10.26
Пров.					
ГИП					
Н. контр.					
Утв.					

ГД-2026-011-АИ

Квартира 56 м²

ЖК «Северный парк», Москва

Дизайн-проект интерьера

Стадия	Лист	Листов
РП	32	83

Схема разводки водопровода и канализации

М б/м

Кырлан Александр Сергеевич

выпуск 19.10.2026 № 1c3e34763b · стр. 39 из 117

Спецификация сантехнического оборудования

Форма 1 ГОСТ 21.110-2013 · ГД-2026-011-АИ-ВК.СО · приборы, арматура, трубопроводы

ПРЕДВАРИТЕЛЬНО · не для производства работ · открыто пунктов: 10 (реестр — л. 5)

Поз.	Наименование и техническая характеристика	Тип, марка, обозначение документа	Код продукции	Поставщик	Ед. изм.	Кол.	Масса 1 ед., кг	Примечание
	Санитарные приборы							
1	Ванна акриловая 1700×750 мм, с каркасом, экраном и отверстием слив-перелив	аналог		выбор заказчика	шт	1		Сн1
2	Унитаз подвесной безободковый, с сиденьем микролифт, крепёж и звукоизолирующая прокладка	Laufen Pro 8.2096.6.000.000.1		выбор заказчика	шт	1		Сн2
3	Инсталляция для подвесного унитаза: рама высотой 1120 мм, бачок, клавиша смыва (ось клавиши 1050 мм от чистого пола)	аналог		выбор заказчика	шт	1		Сн2; короб ГКЛВ
4	Умывальник подвесной 600×450 мм, с отверстием под смеситель и переливом	аналог		выбор заказчика	шт	1		Сн3
5	Мойка врезная, нержавеющая сталь, чёрная 500×450 мм, с переливом	аналог		с кухонной мебелью	шт	1		П1
6	Полотенцесушитель электрический, IP44, с терморегулятором	аналог		выбор заказчика	шт	1		Сн5
	Смесители, сифоны и арматура приборов							
7	Смеситель для ванны настенный однорычажный, межосевое 150 мм, с душевым набором (лейка, шланг, держатель)	аналог		выбор заказчика	шт	1		Сн1
8	Смеситель для умывальника однорычажный, с донным клапаном	аналог		выбор заказчика	шт	1		Сн3
9	Смеситель кухонный однорычажный, высокий излив	аналог		выбор заказчика	шт	1		П1
10	Обвязка ванны слив-перелив Ø40/50 с сифоном	аналог		выбор заказчика	шт	1		Сн1
11	Сифон для умывальника бутылочный Ø32/40–50, с гофрой к выпуску	аналог		выбор заказчика	шт	1		Сн3
12	Сифон для мойки с отводом для ПММ Ø40/50	аналог		выбор заказчика	шт	1		П1
13	Сифон для стиральной машины встраиваемый в стену Ø50, с обратным клапаном	аналог		выбор заказчика	шт	1		Сн4
14	Кран угловой ½"×½" с гибкой подводкой 40 см (умывальники, мойка)	аналог		выбор заказчика	шт	4		по 2 на прибор
15	Кран шаровой угловой ½"×¾" для подключения стиральной и посудомоечной машины	аналог		выбор заказчика	шт	2		Сн4, П2
	Трубопроводы							
16	Труба полипропиленовая PP-R PN20 Ø20×3,4 (В1)	ГОСТ 32415-2013		выбор заказчика	м	21,5	0,17	15,8 + 3,4 + 10 %
17	Труба PP-R, армированная стекловолокном, PN20 Ø20×2,8 (Т3)	ГОСТ 32415-2013		выбор заказчика	м	19	0,15	14,9 + 2,0 + 10 %
18	Труба канализационная ПП Ø40 (К1)	ГОСТ 32414-2013		выбор заказчика	м	1		0,3 + 0,6 + 10 %
19	Труба канализационная ПП Ø50 (К1)	ГОСТ 32414-2013		выбор заказчика	м	23,5		19,6 + 1,6 + 10 %
20	Труба канализационная ПП Ø110 (К1)	ГОСТ 32414-2013		выбор заказчика	м	1		0,7 + 0,2 + 10 %
	Фасонные части и выводы							
21	Отвод канализационный ПП 45° Ø40	ГОСТ 32414-2013		выбор заказчика	шт	2		2 шт. на поворот
22	Отвод канализационный ПП 45° Ø50	ГОСТ 32414-2013		выбор заказчика	шт	16		2 шт. на поворот
23	Отвод канализационный ПП 45° Ø110	ГОСТ 32414-2013		выбор заказчика	шт	4		2 шт. на поворот
24	Тройник канализационный ПП 45° (врезки ветвей)	ГОСТ 32414-2013		выбор заказчика	шт	5		
25	Ревизия канализационная ПП (после поворота трассы)	ГОСТ 32414-2013		выбор заказчика	шт	6		доступ сохранить
26	Фитинги PP-R Ø20: тройники, угольники 90° (ветви и повороты В1, Т3)	ГОСТ 32415-2013		выбор заказчика	шт	23		
27	Водорозетка PP-R Ø20×½" настенная, с креплением	ГОСТ 32415-2013		выбор заказчика	шт	9		коды — лист выводов
	Узлы ввода, люки, короба							
28	Кран шаровой латунный Ду15 PN16 (отключение ввода)	аналог		выбор заказчика	шт	2		Ст В1-1*, Ст Т3-1*
29	Фильтр сетчатый косой Ду15	аналог		выбор заказчика	шт	2		
30	Счётчик воды крыльчатый Ду15 (ХВ, ГВ), с поверкой	аналог		выбор заказчика	шт	2		пломба УК
31	Клапан обратный Ду15	аналог		выбор заказчика	шт	2		
32	Люк ревизионный нажимной под плитку 300×400 мм	аналог		выбор заказчика	шт	1		к стоякам и арматуре
33	Звукоизоляция стояка К1 в коробе: рулонный звукоизоляционный материал ≥ 10 мм, обмотка стояка на высоту этажа	аналог		выбор заказчика	м	2,7		Ст К1-1*
34	Короб К1 над полом: профиль ПН/ПС, ГКЛВ 12,5 мм под плитку	аналог		выбор заказчика	м	16		сечение — лист разводки

Примечания

1. Форма 1 ГОСТ 21.110-2013, ширины граф изменены по п. 4.1. «Аналог» — аналог по характеристикам: модели внести до черновых работ, привязки выводов сверить по паспортам.
2. Бытовая техника не входит (показана арматура подключения), мойка — в комплекте кухни. Длины труб — трасса листа разводки + подъёмы + 10 %.
3. Стояк К1 в коробе — звукоизоляция стояка в коробе без жёсткого контакта короба с трубой. Стояки со «*» (Ст К1-1*, Ст В1-1*, Ст Т3-1) приняты положение и число узлов ввода сверить на объекте.
4. Расчёт систем водоснабжения и канализации, диаметры магистралей и подбор оборудования выполняет проектная организация.

Допущения и предложения на листе

Основа листа: размеры помещений и положение проёмов введены заказчиком в брифе, на объекте не замерены (К-1); высота потолка 2700 мм — по брифу заказчика, не замерена (К-2); толщины стен приняты по брифу: наружные 200 мм, внутренние 150 мм — не обмерены (К-1); тип дома монолитный, перекрытие 200 мм — по брифу заказчика, документов нет (К-3); планировка (стены, проёмы, объединение кухни и гостиной, расширение санузла) — по брифу без обмера и плана БТИ (К-7); разрешённая мощность 10 кВт принята, ТУ не переданы (К-8); вентканалы приняты, в брифе не заданы (К-9); подрайон климата не задан — принят не северный (жилые от 2,5 м) (К-10).

Знак «*» — принято, не замерено и не подтверждено (замерить на объекте): К-4: Ст К1-1 — положение стояка канализации — по брифу заказчика, не замерено; Ст В1-1 — положение стояка холодной воды — по брифу заказчика, не замерено.

См. лист открытых вопросов (лист 5, записи К-1–К-4, К-7–К-10).

Изм.	Кол.уч	Лист	№ док.	Подп.	Дата

Разраб.	Кырлан А.С.	21.10.26
Пров.		
ГИП		
Н. контр.		
Утв.		

ГД-2026-011-АИ

Квартира 56 м²

ЖК «Северный парк», Москва

Дизайн-проект интерьера

Стадия	Лист	Листов
РП	33	83

Спецификация сантехнического оборудования

М б/м

Кырлан Александр Сергеевич

выпуск 19.10.2026 № 1c3e34763b · стр. 40 из 117

Спецификация светильников и сценарии освещения

Светильники, ленты и блоки питания, слои света и сценарии по помещениям · б/м

Спецификация светильников

Поз.	Марки	Наименование	Установка	Кол.	P, Вт	Σ P, Вт	Ф, лм	Тц, К	Ra	Угол, °	IP	Дим.	Группа	Пом.
1	Св31–Св38	Встраиваемый точечный	в ГКЛ, корпус ≤ 70 мм	8	12	96	1000	3000	90	—	20	да	L12	1
2	Св41	Лента светодиодная 24 В	в нише уровня, профиль с рассеивателем	6,4 м	9,6/м	61,4	900/м	2700	90	—	20	да	L13	1
3	Св42**, Св43**, Св44**	Подвесной	подвес, низ H=1450	3	9	27	800	3000	90	—	20	да	L14	1
4	Св45–Св48	Встраиваемый точечный	в ГКЛ, корпус ≤ 70 мм	4	10	40	900	3000	90	—	20	да	L15	1
5	Св49**	Линейный настенный	под верхними шкафами, H=1440	1	18	18	1500	3000	90	—	20	да	L16	1
6	Св1–Св8	Встраиваемый точечный	в ГКЛ, корпус ≤ 70 мм	8	12	96	1000	2700	90	—	20	—	L1	2
7	Св9	Лента светодиодная 24 В	в карнизе короба, профиль с рассеивателем	11,7 м	9,6/м	112,3	900/м	2700	90	—	20	да	L2	2
8	Св10, Св11, Св24, Св25	Настенный (бра)	на стене, H=1500	4	6	24	400	2700	90	60	20	—	L3, L9	2, 3
9	Св17–Св22	Встраиваемый точечный	в ГКЛ, корпус ≤ 70 мм	6	12	72	1050	2700	90	—	20	—	L7	3
10	Св23	Лента светодиодная 24 В	в карнизе короба, профиль с рассеивателем	8,7 м	9,6/м	83,5	900/м	2700	90	—	20	да	L8	3
11	Св12–Св14	Встраиваемый точечный	в ГКЛ, корпус ≤ 70 мм	3	6	18	500	3000	90	—	44	—	L4	4
12	Св15	Настенный светильник над зеркалом, драйвер встроен	над зеркалом, H=1900	1	8	8	600	3000	90	—	44	—	L5	4
13	Св26–Св29	Встраиваемый точечный	в ГКЛ, корпус ≤ 70 мм	4	7	28	600	3000	90	—	20	—	L10	5
14	Св30	Лента светодиодная 24 В	в коробе, профиль с рассеивателем, датчик движения	1,8 м	4,8/м	8,6	150/м	2700	90	—	20	нет	L11	5
		Итого		**42 шт + 28,6 м**		**692,9**								

Слои света по помещениям

Пом.	Помещение	Слои света и группы включения (марки светильников)	Тц, К	Ra	Σ P, Вт	Сцен.
1	Гостиная-кухня	общий — L12 (Св31–Св38), L14 (Св42**, Св43**, Св44**), L15 (Св45–Св48); рабочий — L16 (Св49**); акцентный — L13 (Св41)	2700 / 3000	90	242,4	4
2	Спальня	общий — L1 (Св1–Св8); рабочий — L3 (Св10, Св11); акцентный — L2 (Св9)	2700	90	220,3	2
3	Детская	общий — L7 (Св17–Св22); рабочий — L9 (Св24, Св25); акцентный — L8 (Св23)	2700	90	167,5	1
4	Санузел	общий — L4 (Св12–Св14); рабочий — L5 (Св15)	3000	90	26	—
5	Прихожая	общий — L10 (Св26–Св29); ночной — L11 (Св30)	2700 / 3000	90	36,6	—

LED-ленты, линейные светильники и блоки питания

Марка	Пом.	L, м	U, В	Вт/м	Σ P, Вт	БП	P БП, Вт	Загр., %	Питание	Доступ к БП
Св41	1	6,4	24	9,6	61,4	БП4	300	20	с двух концов	люк 300×300 в нише фигуры потолка У2
Св49**	1	3	24	—	18	БП5**	60	30	встроенный ввод	в пенале М6, верх, съёмная панель
Св9	2	11,7	24	9,6	112,3	БП1	200	56	с двух концов	люк 300×300 в коробе потолка У1
Св23	3	8,7	24	9,6	83,5	БП2	200	42	с двух концов	люк 300×300 в коробе потолка У1
Св30	5	1,8	24	4,8	8,6	БП3	20	43	с одного конца	в шкафу Пр1, верхняя полка

Сценарии освещения

Пом.	Сценарий	Группы и уровни, %	Чем включается
1	Вечер	L12 споты гостиной — 30; L13 подсветка короба — 100; L14 подвесы над столом — 50; L15 споты кухни — 0; L16 подсветка столешницы — 0	S10 светорегулятор, S11** светорегулятор
1	Ужин	L12 споты гостиной — 0; L13 подсветка короба — 60; L14 подвесы над столом — 100; L15 споты кухни — 0; L16 подсветка столешницы — 30	S10 светорегулятор, S11** светорегулятор, S12** светорегулятор
1	Кино	L12 споты гостиной — 0; L13 подсветка короба — 20; L14 подвесы над столом — 0; L15 споты кухни — 0; L16 подсветка столешницы — 0	S10 светорегулятор
1	Готовка	L12 споты гостиной — 50; L13 подсветка короба — 0; L14 подвесы над столом — 0; L15 споты кухни — 100; L16 подсветка столешницы — 100	S10 светорегулятор, S11** светорегулятор, S12** светорегулятор
2	Вечер	L1 споты — 0; L2 подсветка короба — 100; L3 бра — 100	S1, S2, S3
2	Уборка	L1 споты — 100; L2 подсветка короба — 100; L3 бра — 0	S1, S2, S3
3	Вечер	L7 споты — 0; L8 подсветка короба — 100; L9 бра — 100	S4, S5, S6

Слои света

общий — равномерный свет помещения, по норме освещённости

рабочий — местный свет задачи: столешница, зеркало, чтение у кровати

акцентный — подсветка потолка, стен и ниш; не входит в поток общего света

ночной — путь спальня → санузел: не выше 2700 K, малая яркость, датчик движения

Допущения и предложения на листе

Основа листа: размеры помещений и положение проёмов введены заказчиком в брифе, на объекте не замерены (К-1); высота потолка 2700 мм — по брифу заказчика, не замерена (К-2); толщины стен приняты по брифу: наружные 200 мм, внутренние 150 мм — не обмерены (К-1); тип дома монолитный, перекрытие 200 мм — по брифу заказчика, документов нет (К-3); планировка (стены, проёмы, объединение кухни и гостиной, расширение санузла) — по брифу без обмера и плана БТИ (К-7); разрешённая мощность 10 кВт принята, ТУ не переданы (К-8); вентканалы приняты, в брифе не заданы (К-9); подрайон климата не задан — принят не северный (жилые от 2,5 м) (К-10).

Знак «**» — предложение проектировщика, заказчиком не утверждено (согласовать с заказчиком): записи в реестре нет: S11, S12 — светорегулятор добавлен разработчиком проекта; Св42, Св43, Св44, Св49, БП5 — диммируемость добавлена разработчиком проекта под светорегуляторы S11 и S12.

См. лист открытых вопросов (лист 5, записи К-1–К-3, К-7–К-10).

Примечания

1. Позиции и марки Св — те же, что на плане освещения (лист 22) и в ведомости светильников (лист 24); группы L — по плану выключателей (лист 23).
2. Модели светильников не назначены: подбор по графам спецификации — поток, Тц, Ra, угол, IP и диммирование не хуже указанных, мощность не больше; встраиваемые — под глубину короба (графа «Установка»). IP 20 — сухие помещения.
3. Длина LED-ленты в карнизе и нише уровня — по линиям карниза и ниши плана потолков (лист 36); Σ P = Вт/м × длина. Блок питания загружен не больше чем на 80 %; лента 24 В длиннее 10 м питается с двух концов; доступ к блоку питания — люк ревизии 300×300 мм или место, указанное в таблице.
4. Сценарии: уровень — доля максимальной яркости группы, %; 0 — группа выключена. Уровень ниже 100 % — только у групп на светорегуляторе (задний фронт, ТЕ) с диммируемыми драйверами и блоками питания.
5. Мощность и поток — по паспортам принятых изделий, Σ P — установленная мощность освещения. Оценка освещённости — на плане освещения; это не светотехнический расчёт.

Изм.	Кол.уч	Лист	№ док.	Подп.	Дата
Разраб.		Кырлан А.С.			21.10.26
Пров.					
ГИП					
Н. контр.					
Утв.					

ГД-2026-011-АИ

Квартира 56 м²

ЖК «Северный парк», Москва

Дизайн-проект интерьера

Стадия	Лист	Листов
РП	34	83

Спецификация светильников и сценарии освещения

М б/м


Кырлан Александр Сергеевич

выпуск 19.10.2026 № 1c3e34763b · стр. 41 из 117

Схема каркаса перегородки П-2**

С112; вид, сечения и узлы: каркас, обрамление проёма и примыкания


Вид на каркас без обшивки (М 1:25)

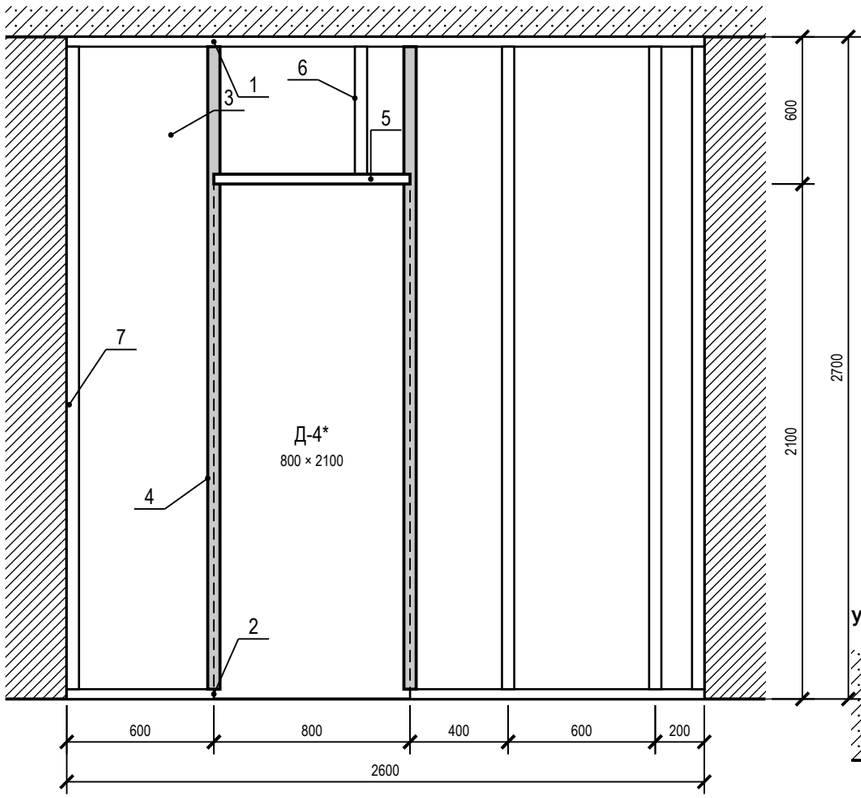

Оси — стойки каркаса; полки профиля на виде условны

Сечение А–А по стойке (М 1:5)


сверху — пом. 3, окраска

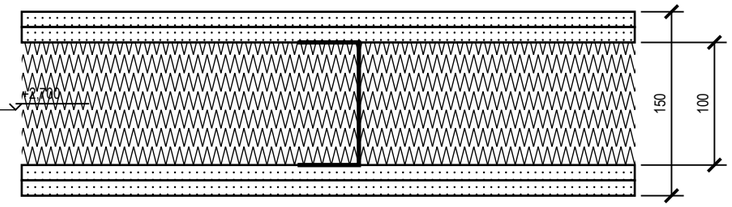

снизу — пом. 5, окраска

поз. 9 — ГКЛ 12,5 мм в 2 слоя с каждой стороны; поз. 3 — ПС 100; поз. 8 — минвата 100 мм (принято)

Сечение Б–Б у проёма, на уровне ниже перемычки (М 1:5)

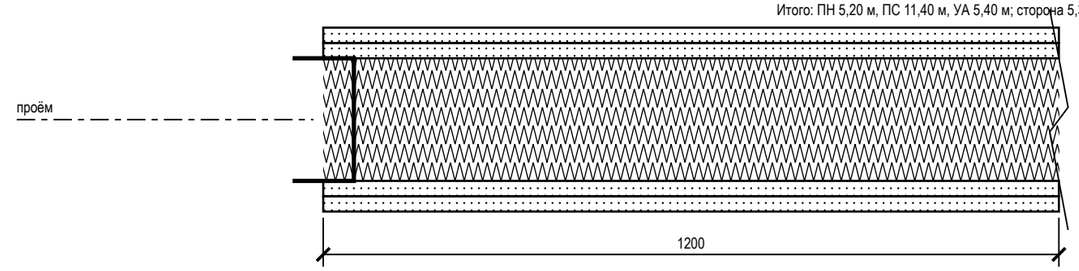


поз. 4 — УА 100, обрамление проёма; обшивка по краю проёма, простенок 1200 мм до пилона (на сечении показан с обрывом)

Ведомость элементов каркаса


Поз.	Наименование	Кол-во	Ед.
1	ПН 100 по потолку (по плите)	2,60	м
2	ПН 100 по полу, без проёма	1,80	м
3	ПС 100 через 600 мм	4 × 2,70	м
4	УА 100 по краям проёма	2 × 2,70	м
5	ПН 100 перемычка над проёмом	0,80	м
6	ПС 100 над перемычкой	1 × 0,60	м
7	Лента уплотнительная под профили	9,80	м
8	Минвата в полость, 100 мм	5,34	м²
9	ГКЛ 12,5 мм, 2 слоя с двух сторон	21,36	м²

Итого: ПН 5,20 м, ПС 11,40 м, УА 5,40 м; сторона 5,34 м²

Узел 1. К плите (М 1:5)

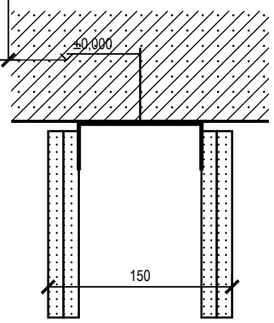

Узел 2. К полу (М 1:5)

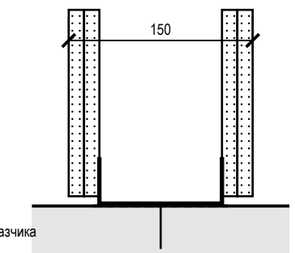

Примечания

1. П-2** (С112, ГКЛ в 2 слоя с каждой стороны, толщина 150 мм, высота 2700 мм до плиты) — предложение проектировщика, автором не утверждено (К-5); ось и длина 2600 мм — со скана плана заказчика (контрольный обмер не выполнялся).
2. Шаг стоек 600 мм — по данным (под плитку и во влажной зоне). Размеры сечений профилей — «ПС 100», «УА 100» по данным и каталогу; толщины листов — ГОСТ 32614-2012.
3. Принято: шаг стоек 600 мм принят по базовому правилу: в данных studStep не задан.
4. Принято: проём Д-4 в каркасе 800 × 2100 мм принят по размеру полотна: короб скрытой двери (модель, размеры) не выбран — проём пересчитать по коробке до монтажа УА (К-5).
5. Принято: перемычка над проёмом — направляющий профиль по верху проёма на всю его ширину; короткие стойки ПС над перемычкой на шаге каркаса: по практике узла Knauf, не по данным объекта (К-5).
6. Принято: заполнение полости — минераловатная плита на всю глубину профиля (Rw системы С112 нормируют с заполнением); марка и плотность выбираются при закупке (К-5).
7. Принято: длина стойки равна высоте перегородки: стойки режут на высоту между направляющими при монтаже, зазоры до плиты и пола в данных не заданы (edgeGaps).
8. Обшивку крепят к стойкам шурупами через слой, швы слоёв вразбежку; зазоры обшивки до плиты и пола, шаг дюбелей, марка заполнения — по ТУ системы и узлу изготовителя.

Допущения и предложения на листе

Основа листа: размеры помещений и положение проёмов введены заказчиком в брифе, на объекте не замерены (К-1); высота потолка 2700 мм — по брифу заказчика, не замерена (К-2); толщины стен приняты по брифу: наружные 200 мм, внутренние 150 мм — не обмерены (К-1); тип дома монолитный, перекрытие 200 мм — по брифу заказчика, документов нет (К-3); планировка (стены, проёмы, объединение кухни и гостиной, расширение санузла) — по брифу без обмера и плана БТИ (К-7); разрешённая мощность 10 кВт принята, ТУ не переданы (К-8); вентканалы приняты, в брифе не заданы (К-9); подрайон климата не задан — принят не северный (жилые от 2,5 м) (К-10).

Знак «**» — предложение проектировщика, заказчиком не утверждено (согласовать с заказчиком): К-5: П-2 — положение, материал (ГКЛ) и толщина 150 мм — по брифу заказчика; конструкция (система С112, 2 слоя с каждой стороны, Rw 51 дБ — нижняя граница диапазона системы С112 (51–56 дБ)) — выбор исполнителя, автором не утверждена.

См. лист открытых вопросов (лист 5, записи К-1–К-3, К-5, К-7–К-10).

Изм.	Кол.уч	Лист	№ док.	Подп.	Дата
Разраб.		Кырлан А.С.			21.10.26
Пров.					
ГИП					
Н. контр.					
Утв.					

ГД-2026-011-АИ

Квартира 56 м²

ЖК «Северный парк», Москва

Дизайн-проект интерьера

Стадия	Лист	Листов
РП	35	83

Схема каркаса перегородки П-2

по видам

Кырлан Александр Сергеевич

выпуск 19.10.2026 № 1c3e34763b · стр. 42 из 117

06

Потолки и ГКЛ-конструкции


Кырлан Александр Сергеевич

выпуск 19.10.2026 · 1c3e34763b · стр. 43 из 117

План потолков

Уровни и марки потолков, короба с подсветкой, ниши под шторы, люки, вырезы · отметки низа от ±0,000 чистого пола · размеры в мм

ПРЕДВАРИТЕЛЬНО · не для производства работ · открыто пунктов: 10 (реестр — л. 5)

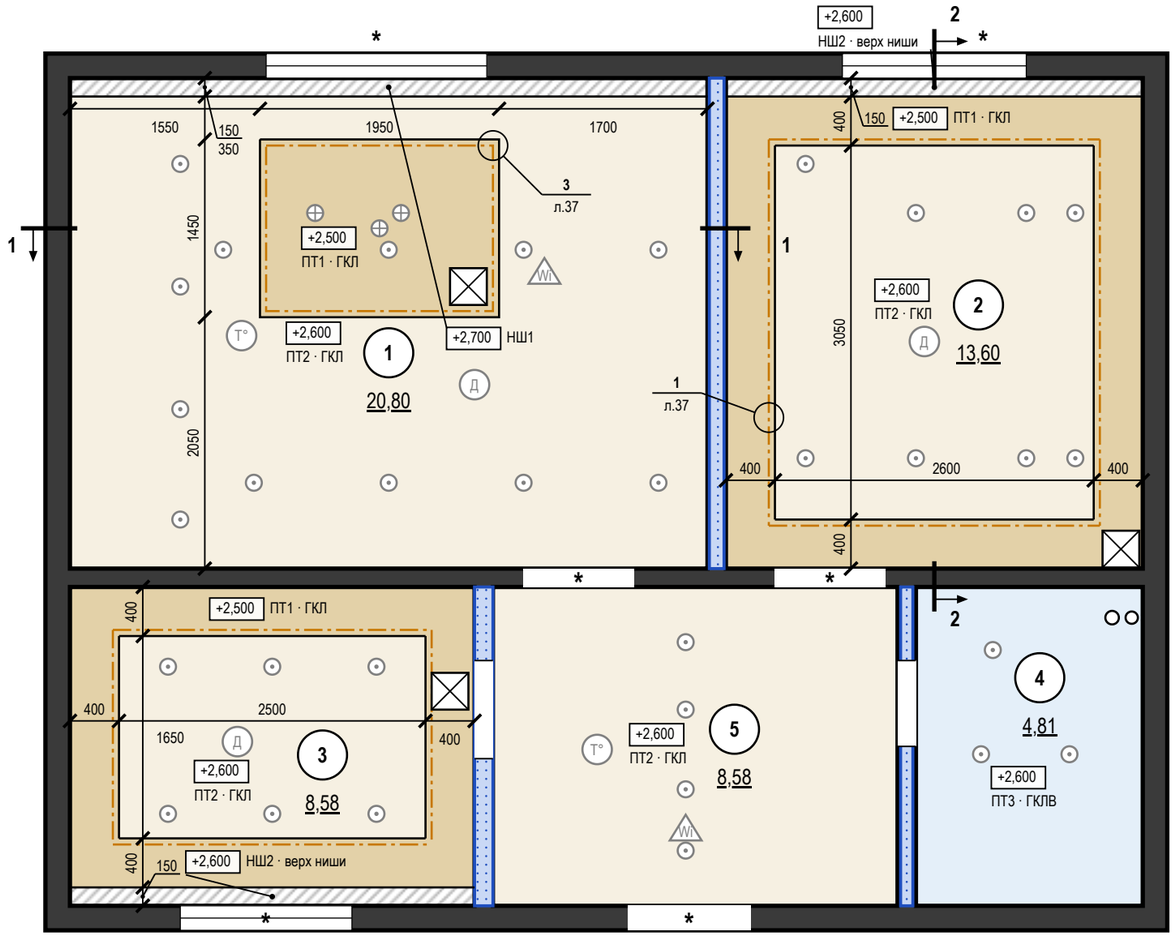

Ведомость потолков

Пом.	Марка	Конструкция	Низ / верх ниши	S, м²	Q
1	ПТ1	ГКЛ П113, остров + LED	+2,500	2,83	Q3
1	ПТ2	ГКЛ П113	+2,600	17,19	Q3
1	НШ1	ниша под шторы 150×100	+2,700	0,78	
2	ПТ1	ГКЛ П113, короб LED	+2,500	5,16	Q3
2	ПТ2	ГКЛ П113	+2,600	7,93	Q3
2	НШ2	ниша под шторы 150×100	+2,600	0,51	
3	ПТ1	ГКЛ П113, короб LED	+2,500	3,96	Q3
3	ПТ2	ГКЛ П113	+2,600	4,13	Q3
3	НШ2	ниша под шторы 150×100	+2,600	0,49	
4	ПТ3	ГКЛВ П113	+2,600	4,81	Q3
5	ПТ2	ГКЛ П113	+2,600	8,58	Q3
		Итого		**56,37**	

Ведомость вырезов и закладных в потолке

Марка	Устройство	Кол.	Пом.
	Светильник встраиваемый (марки — план освещения)	33	1, 2, 3, 4, 5
	Светильник подвесной (марки — план освещения)	3	1
ИП4, ИП1, ИП2	Извещатель дымовой	3	1, 2, 3
ИП5, ИП3	Извещатель тепловой	2	1, 5
АР2**, АР1**	Точка доступа Wi-Fi, PoE	2	1, 5
	Люк ревизии 300×300	3	1, 2, 3

Условные обозначения

- ПТ1 — ГКЛ по каркасу П113, низ +2,500
- ПТ2 — ГКЛ по каркасу П113, низ +2,600
- ПТ3 — ГКЛВ по каркасу П113, низ +2,600
- НШ1 — ниша под шторы 150×100, верх +2,700
- НШ2 — ниша под шторы 150×100, верх +2,600
- граница уровней потолка (перепад)
- LED-лента в нише подсветки (карниз короба, ниша фигуры)
- стояк: К1 — канализация, В1 — ХВС, Т3 — ГВС
- люк ревизии в потолке 300×300 мм (доступ к БП LED)
- светильник встраиваемый — подложка с плана освещения
- светильник подвесной — подложка с плана освещения

Условные обозначения (продолжение)

- Д — извещатель дымовой на потолке — подложка
- Т° — извещатель тепловой на потолке — подложка
- Wi — точка доступа Wi-Fi на потолке — подложка
- линия разреза у стен помещения, стрелка — направление взгляда
- место узла: номер узла на полке, под полкой — лист
- +2,600 — отметка низа потолка, м (у ниши под шторы — верх ниши); под ней марка потолка
- новое — возводится по проекту (синим)
- 1 — номер помещения, площадь м²

Допущения и предложения на листе. Знак «*» принято (замерить): Ст К1-1, Ст В1-1. Знак «**» предложено (согласовать): П-1, П-2, П-3. См. лист открытых вопросов (лист 5).

Примечания

1. За отметку ±0,000 принят уровень чистого пола сухих помещений (готовое покрытие), а не существующего пола; пол пом. 4 — −0,015; верх плиты перекрытия −0,064 — расчётный по пирогу пола, не замерен; существующий пол снимается до плиты, его отметка не замерена. Отметки в прямоугольниках — низ потолка; низ плиты перекрытия +2,700. Марка потолка — одна конструкция и отметка на весь альбом.
2. Потолки ГКЛ — каркасная система П113: подвесы через 1000 (с запасом: СП 163, табл. 14 — до 1100 при 0,15 кН/м²), несущие профили через 500, основные через 1200 мм; листы — поперёк несущих профилей. В помещениях 4 — ГКЛВ на оцинкованном каркасе.
3. Нижний уровень — пояс-короб по периметру шириной 400 мм, верхний — поле внутри пояса: пом. 2, 3.
4. LED-лента в алюминиевом профиле посередине карниза короба шириной 400 мм (узел 1, лист 37); длина по плану: пом. 2 — 11,7 м (в плане освещения 11,7); пом. 3 — 8,7 м (в плане освещения 8,7).
5. Ниши под шторы 150×100 мм — на всю длину стены с окном; карниз — на закладной до обшивки (узел 2 — пом. 1, лист 37; узел 4 — пом. 2, 3, лист 38).
6. Примыкание к стенам: теневой шов 15 мм, техзазор 3 мм — пом. 1, 2, 3, 5, по стенам, выровненным штукатуркой (узел 1); пом. 4 — разделительная лента.
7. Светильники и потолочные устройства — подложка с планов освещения, слаботочных систем и вентиляции (положение — по ним); вырезы и закладные — по ведомости на листе, до обшивки; отверстия не совмещать с профилями, глубина корпуса светильника до 70 мм.
8. Разрезы 1–1, 2–2 — на листе 37; высоты мебели и дверных блоков сверены с низом потолка в разрезах; гибка бортов фигур и ленты ниш — там же; размеры фигурных уровней — фрагмент 1 (лист 38).
9. Узлы по выноскам на плане: узлы 1, 2, 3 — лист 37; узел 4 — лист 38.
10. Шпаклевание ГКЛ и условия приёмки — Q3: рассеянный дневной свет, осмотр с 2 м; боковой свет не оценивается.
11. Люки ревизии 300×300 мм — по центру блоков питания LED (БП4, БП1, БП2; координаты — план освещения).

1000 мм · печать 1:1

Изм.	Кол.уч	Лист	№ док.	Подп.	Дата
Разраб.		Кырлан А.С.			21.10.26
Пров.					
ГИП					
Н. контр.					
Утв.					

ГД-2026-011-АИ

Квартира 56 м²

ЖК «Северный парк», Москва

Дизайн-проект интерьера

Стадия	Лист	Листов
РП	36	83

План потолков

М 1:50

Кырлан Александр Сергеевич


выпуск 19.10.2026 № 1c3e34763b · стр. 44 из 117

Разрезы и узлы потолков

Разрезы по потолкам с отметками уровней · узлы коробов и ниш · размеры в мм


Разрез 1–1 (М 1:40)

Пом. 1 Гостиная-кухня; линия разреза — план потолков, лист 36

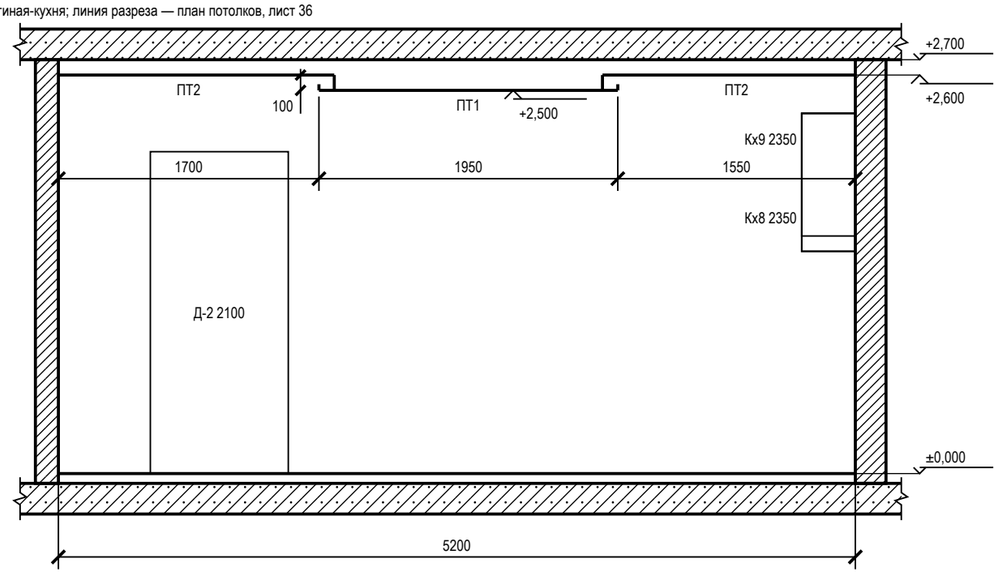


Разрез 2–2 (М 1:40)

Пом. 2 Спальня; линия разреза — план потолков, лист 36

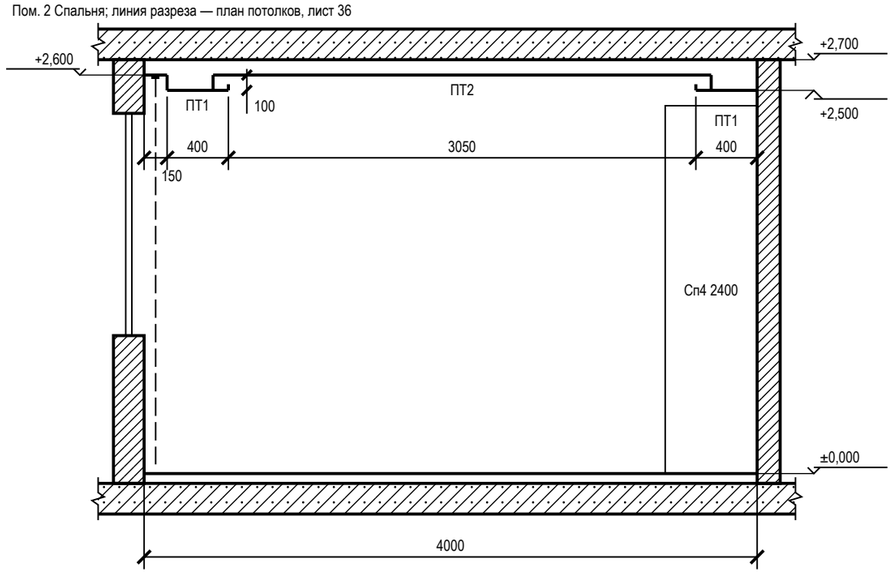

1 Короб с LED-подсветкой, теневой шов (М 1:10)


Пом. 2, 3; карниз 100×100, щель под свет 60 мм

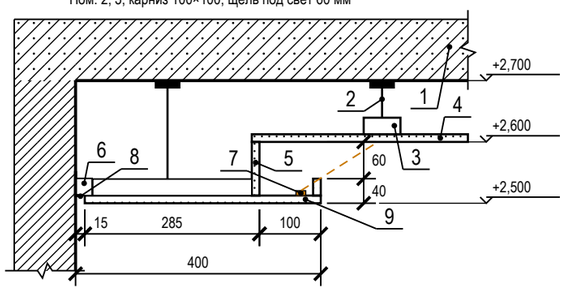

1 — плита перекрытия
2 — подвес прямой, шаг 1000 мм
3 — ПП 60×27: несущие через 500, основные через 1200 мм
4 — ГКЛ 12,5 по П113 — верхний уровень
5 — задняя стенка и бортик карниза — ГКЛ 12,5
6 — ПН 28×27 по периметру, к стене через 500 мм
7 — LED-лента в алюминиевом профиле
8 — теневой профиль: шов 15 мм, зазор 3 мм
9 — низ короба — ГКЛ 12,5 по ПП 60×27

2 Ниша под шторы (М 1:10)


Пом. 1; без подсветки; закладные под карниз — до обшивки

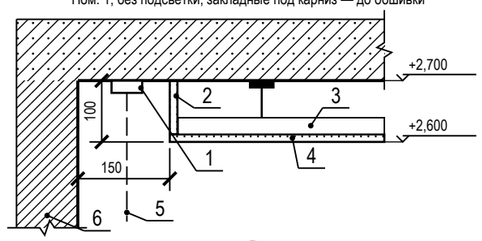

1 — карниз (шина), высота с верхом портьеры 80 мм
2 — стенка ниши — ГКЛ 12,5
3 — ПП 60×27 — каркас короба
4 — низ короба нижнего уровня — ГКЛ 12,5
5 — портьера
6 — стена с окном

3 Ниша LED фигурного уровня (М 1:10)

Пом. 1; карниз 100×100, щель под свет 60 мм

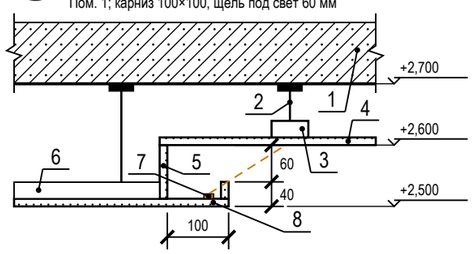

1 — плита перекрытия
2 — подвес прямой, шаг 1000 мм
3 — ПП 60×27: несущие через 500, основные через 1200 мм
4 — ГКЛ 12,5 по П113 — верхний уровень
5 — задняя стенка и бортик карниза — ГКЛ 12,5
6 — ПП 60×27 каркаса нижнего уровня, ПН по контуру фигуры (на дуге — с надрезами)
7 — LED-лента в алюминиевом профиле
8 — низ короба — ГКЛ 12,5 по ПП 60×27

Условные обозначения

- плита перекрытия в сечении
- стена в сечении
- потолок ГКЛ в сечении; под линией — марка потолка (план потолков)
- мебель и дверные проёмы за секущей плоскостью; число — марка и верх от чистого пола, мм
- портьера в нише под шторы

Допущения и предложения на листе

Основа листа: размеры помещений и положение проёмов введены заказчиком в брифе, на объекте не замерены (К-1); высота потолка 2700 мм — по брифу заказчика, не замерена (К-2); толщины стен приняты по брифу: наружные 200 мм, внутренние 150 мм — не обмерены (К-1); тип дома монолитный, перекрытие 200 мм — по брифу заказчика, документов нет (К-3); планировка (стены, проёмы, объединение кухни и гостиной, расширение санузла) — по брифу без обмера и плана БТИ (К-7); разрешённая мощность 10 кВт принята, ТУ не переданы (К-8); вентканалы приняты, в брифе не заданы (К-9); подрайон климата не задан — принят не северный (жилые от 2,5 м) (К-10).
См. лист открытых вопросов (лист 5, записи К-1–К-3, К-7–К-10).

Примечания

1. Разрезы — по линиям 1–1, 2–2 на плане потолков (лист 36). Отметки — от ±0,000 чистого пола, м; размеры — мм.
2. Высоты мебели и дверных блоков за секущей плоскостью сверены с низом потолка над ними: верх ниже низа короба и поля.
3. ГКЛ 12,5 мм по каркасу П113; перепад уровней и бортик карниза — ГКЛ по ПП 60×27 (узел 1 — на этом листе). Ниша под шторы — на всю длину стены с окном, карниз на закладной до обшивки (узел 2 — на этом листе; узел 4 — лист 38).
4. Толщины плит перекрытия и пирога пола показаны условно.
5. Сечения потолков по помещениям М 1:10 (отметки помещения, профили, подвесы, крепёж, изделия) — лист 39.
6. Ведомость объёмов потолков (лист ГКЛ, профиль, подвесы, лента, блоки питания, люки) — на листе 38.
7. Фрагмент 1 — помещение с фигурными уровнями (размеры фигур, радиусы, отметки) — на листе 38.

1000 мм · печать 1:1

Изм.	Кол.уч	Лист	№ док.	Подп.	Дата
Разраб.		Кырлан А.С.			21.10.26
Пров.					
ГИП					
Н. контр.					
Утв.					

ГД-2026-011-АИ

Квартира 56 м²

ЖК «Северный парк», Москва

Дизайн-проект интерьера

Стадия	Лист	Листов
РП	37	83

Разрезы и узлы потолков

М 1:40; 1:10

Кырлан Александр Сергеевич


выпуск 19.10.2026 № 1c3e34763b · стр. 45 из 117

Разрезы и узлы потолков (продолжение)

Узлы коробов и ниш · фрагменты фигурных уровней · ведомость объёмов · размеры в мм

Фрагмент 1. Пом. 1 Гостиная-кухня — уровни потолка (М 1:50)

Цепочки — от чистых граней стен; отметки — низ уровня от ±0,000

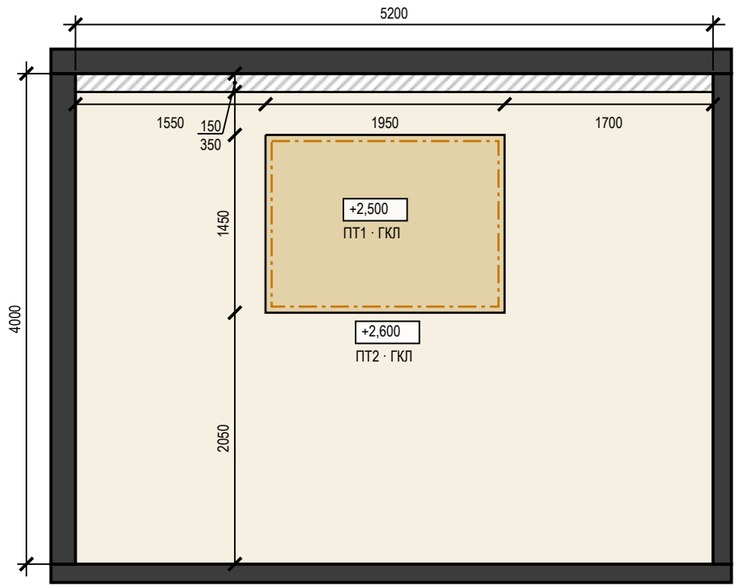

ПТ1 — низ +2,500

ПТ2 — низ +2,600

LED-лента в нише подсветки (карниз короба, ниша фигуры)


ниша под шторы

Ведомость объёмов потолков

Позиция	Ед.	Кол.	Пом.
Лист ГКЛ 12,5	м²	59,20	1, 2, 3, 5
Лист ГКЛВ 12,5	м²	4,81	4
Борта и карнизы (входят в площади листов выше)	м²	7,64	1, 2, 3
Профиль ПП 60×27	м	169,21	1, 2, 3, 4, 5
Профиль ПН 28×27	м	169,50	1, 2, 3, 4, 5
Подвес прямой	шт.	72	1, 2, 3, 4, 5
Анкер-клин к плите	шт.	72	1, 2, 3, 4, 5
Шуруп TN 3,5×25	шт.	1472	1, 2, 3, 4, 5
Лента армирующая для швов	м	76,81	1, 2, 3, 4, 5
Шпаклёвка для швов	кг	25,60	1, 2, 3, 4, 5
Грунтовка (швы)	л	6,40	1, 2, 3, 4, 5
Лента разделительная по периметру	м	65,70	1, 2, 3, 4, 5
Сплошная шпаклёвка и окраска (площадь развёртки)	м²	64,01	1, 2, 3, 4, 5
Лента LED	м	26,80	1, 2, 3
Требуемая мощность блоков питания	Вт	334	1, 2, 3
Установленная мощность блоков питания	Вт	700	1, 2, 3
Блок питания LED	шт.	3	1, 2, 3
Люк ревизии	шт.	3	1, 2, 3

4 Ниша под шторы (М 1:10)

Пом. 2, 3; без подсветки; закладные под карниз — до обшивки

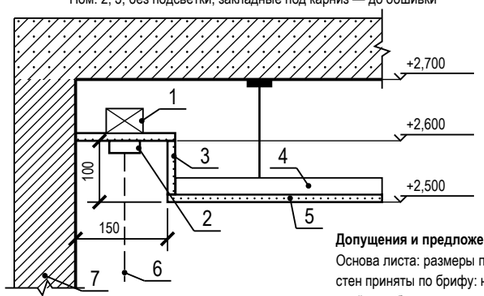

1 — закладная под карниз — брус 40×50

2 — карниз (шина), высота с верхом портьеры 80 мм

3 — стенка и потолок ниши — ГКЛ 12,5

4 — ПП 60×27 — каркас короба

5 — низ короба нижнего уровня — ГКЛ 12,5

6 — портьера

7 — стена с окном

Допущения и предложения на листе

Основа листа: размеры помещений и положение проёмов введены заказчиком в брифе, на объекте не замерены (К-1); высота потолка 2700 мм — по брифу заказчика, не замерена (К-2); толщины стен приняты по брифу: наружные 200 мм, внутренние 150 мм — не обмерены (К-1); тип дома монолитный, перекрытие 200 мм — по брифу заказчика, документов нет (К-3); планировка (стены, проёмы, объединение кухни и гостиной, расширение санузла) — по брифу без обмера и плана БТИ (К-7); разрешённая мощность 10 кВт принята, ТУ не переданы (К-8); вентканалы приняты, в брифе не заданы (К-9); подрайон климата не задан — принят не северный (жилые от 2,5 м) (К-10).

См. лист открытых вопросов (лист 5, записи К-1–К-3, К-7–К-10).

Примечания

1. ГКЛ 12,5 мм по каркасу П113; узлы коробов и ниш под шторы: узел 1 — лист 37; узел 2 — лист 37; узел 4 — на этом листе; условные обозначения разрезов — на листе 37.
2. Фрагмент 1 (план потолков — лист 36) — фигурные уровни потолка крупно: привязки краёв и центров фигур к чистым граням стен, радиусы (R) с центрами, хорда и стрелка дуги, отметки низа каждого уровня; цвета уровней — как на плане потолков.
3. Фигурные уровни: борт — ГКЛ по ПН с надрезами (на дуге шаг стоек борта 300 мм при R до 2500, 400 — до 5000) или по гнутому заводскому профилю (СП 163, 6.3.3). Лента в нише фигуры по оси: остров пом. 1 — 6,4 м; узел ниши LED фигуры: узел 3 — лист 37 — пом. 1.
4. Ведомость объёмов — по геометрии плана потолков: Лист ГКЛ 12,5 — плоскости уровней + борта (без арочных участков); Лист ГКЛВ 12,5 — плоскости уровней + борта; Борта и карнизы — длина перепада × перепад; Профиль ПП 60×27 — S × (1/шаг несущ. + 1/шаг осн.) + стойки бортов; Профиль ПН 28×27 — периметр стен + 2 × перепады + карнизы; Подвес прямой — по раскладке: S уровня / (шаг осн. × шаг подвесов), пояс уже шага — ряд вдоль пояса, фигура — по контуру; шаг подвесов — не больше табл. 14 СП 163; Анкер-клин к плите — по одному на подвес (Knauf П113); Шуруп TN 3,5×25 — 23 шт./м² (Knauf П113, табл. 2 альбома П 11); Лента армирующая для швов — 1,2 м/м² листа (Knauf); Шпаклёвка для швов — 0,4 кг/м² листа, только швы (Knauf); Грунтовка (швы) — 0,1 л/м² листа, только швы (Knauf); Лента разделительная по периметру — периметр стен под потолком ГКЛ; Сплошная шпаклёвка и окраска (площадь развёртки) — плоскости + борта; расход — по паспорту материала (норма на сплошной слой не подтверждена, knowledge/ceilings.md 2.3); Лента LED — по оси карниза и ниши фигуры (план потолков); Требуемая мощность блоков питания — Вт/м × длина × 1,3; Установленная мощность блоков питания — сумма мощностей блоков по плану освещения; Блок питания LED — блоки потолочных лент по плану освещения (БП4, БП1, БП2); Люк ревизии — план потолков; без запаса на подрезку (при закупке листа: ×1,075 при S > 20 м², ×1,175 — 10–20 м², ×1,275 — < 10 м²).

1000 мм · печать 1:1

Изм.	Кол.уч	Лист	№ док.	Подп.	Дата
Разраб.		Кырлан А.С.			21.10.26
Пров.					
ГИП					
Н. контр.					
Утв.					

ГД-2026-011-АИ

Квартира 56 м²

ЖК «Северный парк», Москва

Дизайн-проект интерьера

Стадия	Лист	Листов
РП	38	83

Разрезы и узлы потолков (продолжение)

М 1:50; 1:10

Кырлан Александр Сергеевич


выпуск 19.10.2026 № 1c3e34763b · стр. 46 из 117

Разрезы и узлы потолков (продолжение)

Сечения потолков М 1:10 · пом. 1, 2, 3 · профили, подвесы, крепёж, изделия · размеры в мм

Сечение 1.1. Ниша LED фигурного уровня (М 1:10)


Пом. 1 Гостиная-кухня; карниз 100×100, щель под свет 60 мм

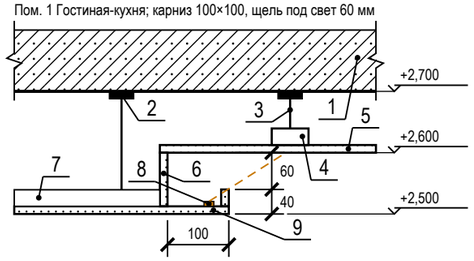

1 — плита перекрытия
2 — анкер-клин к плите — по одному на подвес
3 — подвес прямой, шаг 1000 мм
4 — ПП 60×27: несущие через 500, основные через 1200 мм; соединители одноуровневые, шурупы LN 3,5×9
5 — ГКЛ 12,5 по П113 — верхний уровень; шурупы TN 3,5×25 через 170 мм
6 — задняя стенка и бортик карниза — ГКЛ 12,5
7 — ПП 60×27 каркаса нижнего уровня, ПН по контуру фигуры (на дуге — с надрезами)
8 — LED-лента 9,6 Вт/м, 24 В в алюминиевом профиле
9 — низ короба — ГКЛ 12,5 по ПП 60×27

Сечение 1.2. Ниша под шторы (М 1:10)


Пом. 1 Гостиная-кухня; без подсветки; закладные под карниз — до обшивки

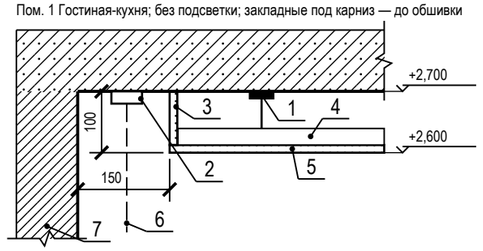

1 — анкер-клин к плите — по одному на подвес; подвес прямой, шаг 1000 мм
2 — карниз (шина), высота с верхом портьеры 80 мм
3 — стенка ниши — ГКЛ 12,5
4 — ПП 60×27 — каркас короба, основные через 1200 мм; соединители одноуровневые, шурупы LN 3,5×9
5 — низ короба нижнего уровня — ГКЛ 12,5; шурупы TN 3,5×25 через 170 мм
6 — портьера
7 — стена с окном

Сечение 1.3. Примыкание потолка к стене (М 1:10)


Пом. 1 Гостиная-кухня; примыкание — теневой шов

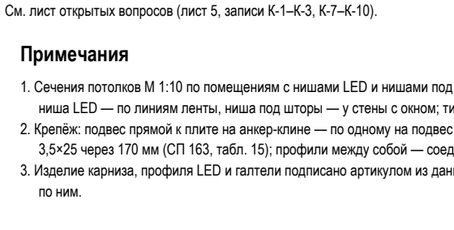

1 — плита перекрытия
2 — анкер-клин к плите — по одному на подвес
3 — подвес прямой, шаг 1000 мм
4 — ПН 28×27 по периметру — дюбель-гвоздь через ≤ 500 мм, не менее 3 на профиль
5 — ПП 60×27 несущий (вид) через 500 мм, в ПН
6 — ПП 60×27 основной (сечение) через 1200 мм; соединители одноуровневые, шурупы LN 3,5×9
7 — теневой профиль: шов 15 мм, зазор 3 мм; стена под шов выровнена
8 — ГКЛ 12,5 по П113; шурупы TN 3,5×25 через 170 мм

Сечение 2.1. Короб с LED-подсветкой, теневой шов (М 1:10)


Пом. 2 Спальня, 3 Детская; карниз 100×100, щель под свет 60 мм

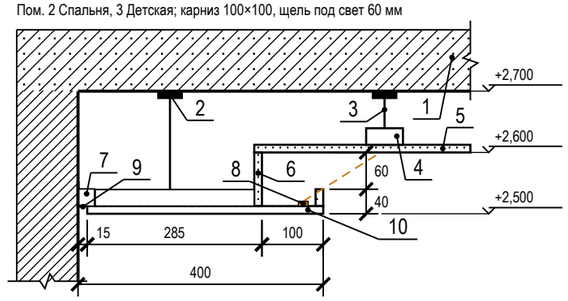

1 — плита перекрытия
2 — анкер-клин к плите — по одному на подвес
3 — подвес прямой, шаг 1000 мм
4 — ПП 60×27: несущие через 500, основные через 1200 мм; соединители одноуровневые, шурупы LN 3,5×9
5 — ГКЛ 12,5 по П113 — верхний уровень; шурупы TN 3,5×25 через 170 мм
6 — задняя стенка и бортик карниза — ГКЛ 12,5
7 — ПН 28×27 по периметру — дюбель-гвоздь через ≤ 500 мм, не менее 3 на профиль
8 — LED-лента 9,6 Вт/м, 24 В в алюминиевом профиле
9 — теневой профиль: шов 15 мм, зазор 3 мм
10 — низ короба — ГКЛ 12,5 по ПП 60×27

Сечение 2.2. Ниша под шторы (М 1:10)

Пом. 2 Спальня, 3 Детская; без подсветки; закладные под карниз — до обшивки

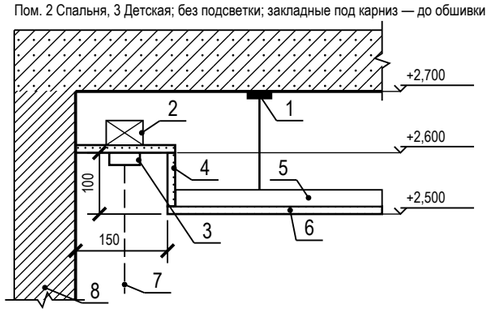

1 — анкер-клин к плите — по одному на подвес; подвес прямой, шаг 1000 мм
2 — закладная под карниз — брус 40×50
3 — карниз (шина), высота с верхом портьеры 80 мм
4 — стенка и потолок ниши — ГКЛ 12,5
5 — ПП 60×27 — каркас короба, основные через 1200 мм; соединители одноуровневые, шурупы LN 3,5×9
6 — низ короба нижнего уровня — ГКЛ 12,5; шурупы TN 3,5×25 через 170 мм
7 — портьера
8 — стена с окном

Условные обозначения

— · — LED-лента в нише подсветки (карниз короба, ниша фигуры)

Допущения и предложения на листе

Основа листа: размеры помещений и положение проёмов введены заказчиком в брифе, на объекте не замерены (К-1); высота потолка 2700 мм — по брифу заказчика, не замерена (К-2); толщины стен приняты по брифу: наружные 200 мм, внутренние 150 мм — не обмерены (К-1); тип дома монолитный, перекрытие 200 мм — по брифу заказчика, документов нет (К-3); планировка (стены, проёмы, объединение кухни и гостиной, расширение санузла) — по брифу без обмера и плана БТИ (К-7); разрешённая мощность 10 кВт принята, ТУ не переданы (К-8); вентканалы приняты, в брифе не заданы (К-9); подрайон климата не задан — принят не северный (жилые от 2,5 м) (К-10).
См. лист открытых вопросов (лист 5, записи К-1–К-3, К-7–К-10).

Примечания

1. Сечения потолков М 1:10 по помещениям с нишами LED и нишами под шторы: отметки и размеры этого помещения от ±0,000 чистого пола (м, мм). Положение — по плану потолков (лист 36): короб и ниша LED — по линиям ленты, ниша под шторы — у стены с окном; типовые узлы по группам помещений — на листе 37.
2. Крепёж: подвес прямой к плите на анкер-клине — по одному на подвес (Knauf П113); ПН к стенам — дюбель-гвоздь через ≤ 500 мм, не менее 3 на профиль (серия 1.045.9-2.08); лист 12,5 — шурупы TN 3,5×25 через 170 мм (СП 163, табл. 15); профили между собой — соединители одноуровневые, шурупы LN 3,5×9.
3. Изделие карниза, профиля LED и галтели подписано артикулом из данных; где артикул не выбран, сечение дано по габаритам из данных (ширина и глубина ниши, щель под свет), изделие подбирается по ним.

1000 мм · печать 1:1

Изм.	Кол.уч	Лист	№ док.	Подп.	Дата
Разраб.		Кырлан А.С.			21.10.26
Пров.					
ГИП					
Н. контр.					
Утв.					

ГД-2026-011-АИ

Квартира 56 м²

ЖК «Северный парк», Москва

Дизайн-проект интерьера

Стадия	Лист	Листов
РП	39	83

Разрезы и узлы потолков (продолжение)

М 1:10

Кырлан Александр Сергеевич


выпуск 19.10.2026 № 1c3e34763b · стр. 47 из 117

Раскладка плитки. Планы полов

Раскладка от чистовых размеров · размеры в мм · отметки от ±0,000

ПРЕДВАРИТЕЛЬНО · не для производства работ · открыто пунктов: 10 (реестр — л. 5)

Фрагмент 1. Санузел (пом. 4). Пол 600×600, шов 2 мм, М 1:20

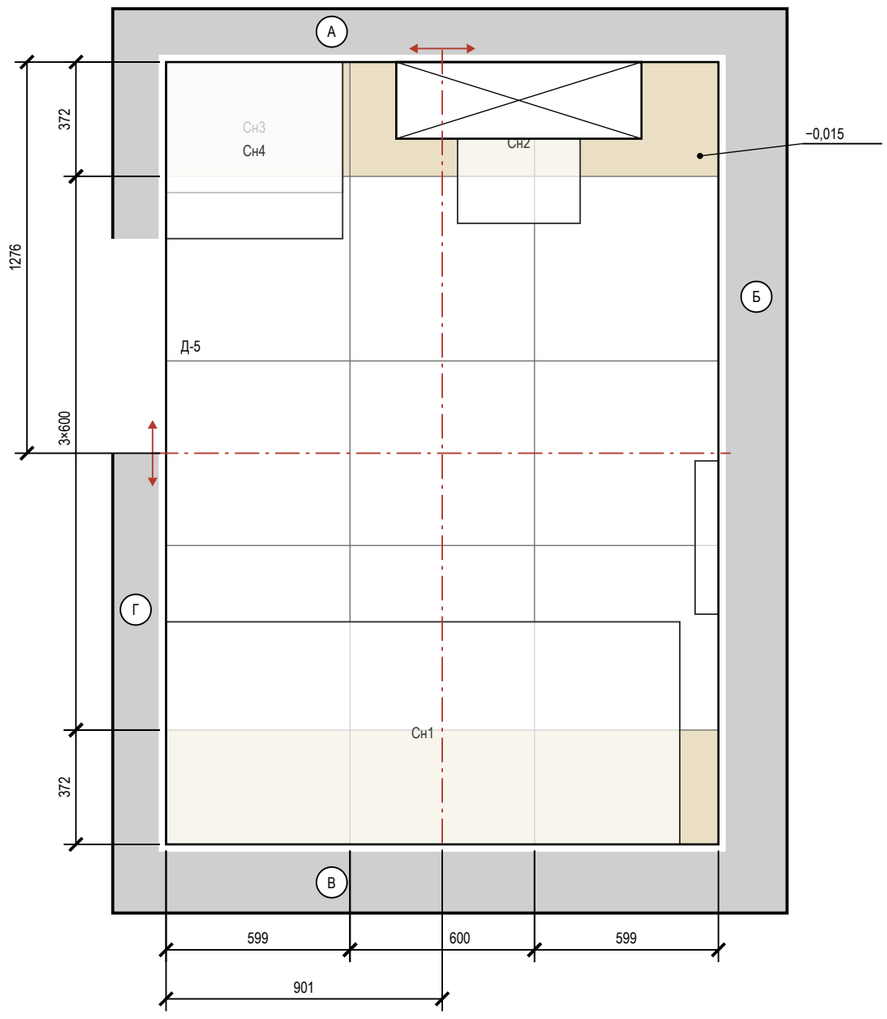

Ведомость плитки

Помещение, поверхность	Плитка, код	Формат	Шов	S, м²	Целых	Подр.	С запасом
Санузел, пол	аналог: керамогранит под травертин	600×600	2	4,81	9	6	17
Санузел, стены А–Г	аналог: керамогранит под травертин	600×1200	2	18,97	18	14	36
Санузел, короб инсталляции	аналог: керамогранит под травертин	600×1200	2	1,76	0	6	7
Прихожая, пол	A8UZ	600×1200	2	8,58	4	14	20
Гостиная-кухня, фартук (ст. Г)	аналог: керамогранит под травертин, матовый	1200×600	2	1,82	0	5	6
Итого 600×600				4,81	9	6	17
Итого 600×1200				**31,13**	**22**	**39**	**69**

Условные обозначения

- плитка целая; тонкая линия — шов
- плитка с подрезкой (размер — на цепочке)
- ось старта; стрелки — направление укладки
- сантехприбор: габарит, высота по практике
- короб инсталляции: плитка пола — до короба
- отметка чистого пола на полке выноски, м
- (А) обозначение стены А–Г (как на развёртках)

Ведомость материалов

Материал	Класс, код	Норма расхода	Кол-во
Затирка	CG2WA Mapei Ultracolor Plus 132	(a+b)/ab·шов·t·1,6	2,1 кг
Затирка	CG2WA	(a+b)/ab·шов·t·1,6	0,8 кг
Клей	C2 TE S1 Ceresit CM 17	1,5 кг/м²·мм, слой 5	204 кг (9 меш.)
Клей	C2 TE S1	1,5 кг/м²·мм, слой 5	85 кг (4 меш.)
Гидроизоляция	обмазочная, 2 слоя: пол, стены по периметру и зоны замачивания	по ТУ	12,4 м²
Демпф. лента	по периметру пола из плитки		16,9 м

Примечания

1. Раскладка от чистовых размеров: стены санузлов теряют 10 + 5 + 9 = 24 мм на сторону (штукатурка, клей, плитка); подрезки — чистые, без шва.
2. Старт — от центра помещения (штрихпунктир, стрелки — направление укладки); размер старта — от чистовых стен Г и А.
3. Раскладка пола «Прихожая» и фартука «Гостиная-кухня» — на листе «Раскладка плитки. Прихожая. Фартук кухни».
4. Калибр партии не задан — до укладки замерить (рабочий размер W, ГОСТ 13996-2019) и пересчитать подрезки.
5. Количество: целые по раскладке + по одной на подрезку, запас 10 %; один артикул — одна партия и тон. Исключены поддон, короб, проёмы и места за коробом; S — по чистым граням: стены нетто = зона облицовки по ведомости отделки − место за коробом инсталляции 0,96 м² (плитку за коробом не кладут), короб — отдельной строкой.
6. Клей C2 TE S1 Ceresit CM 17; C2 TE S1 (ГОСТ Р 56387-2018), затирка CG2WA Mapei Ultracolor Plus 132; CG2WA; расход — по ТУ выбранной марки.
7. Гидроизоляция: пол и стены 200 мм от ЧП; над ванной — до 2000 и 300 мм за борт (см. развёртки); акт скрытых работ, пролив 24 ч.
8. Швы пола совмещены со швами стены А; по периметру — демпферная лента.
9. Отметка чистого пола −0,015, порог 15 мм; стык с соседним покрытием — по оси полотна двери.

Допущения и предложения на листе

Основа листа: размеры помещений и положение проёмов введены заказчиком в брифе, на объекте не замерены (К-1); высота потолка 2700 мм — по брифу заказчика, не замерена (К-2); толщины стен приняты по брифу: наружные 200 мм, внутренние 150 мм — не обмерены (К-1); тип дома монолитный, перекрытие 200 мм — по брифу заказчика, документов нет (К-3); планировка (стены, проёмы, объединение кухни и гостиной, расширение санузла) — по брифу без обмера и плана БТИ (К-7); разрешённая мощность 10 кВт принята, ТУ не переданы (К-8); вентканалы приняты, в брифе не заданы (К-9); подрайон климата не задан — принят не северный (жилые от 2,5 м) (К-10).

См. лист открытых вопросов (лист 5, записи К-1–К-3, К-7–К-10).

1000 мм · печать 1:1

Изм.	Кол.уч	Лист	№ док.	Подп.	Дата
Разраб.		Кырлан А.С.			21.10.26
Пров.					
ГИП					
Н. контр.					
Утв.					

ГД-2026-011-АИ

Квартира 56 м²

ЖК «Северный парк», Москва

Дизайн-проект интерьера

Стадия	Лист	Листов
РП	40	83

Раскладка плитки. Планы полов

М 1:20


Кырлан Александр Сергеевич

выпуск 19.10.2026 № 1c3e34763b · стр. 48 из 117


Раскладка плитки. Прихожая. Фартук кухни

Раскладка от чистовых размеров · размеры в мм · высоты фартука от чистого пола

Фрагмент 1. Прихожая (пом. 5). Пол 600×1200, шов 2 мм, М 1:25

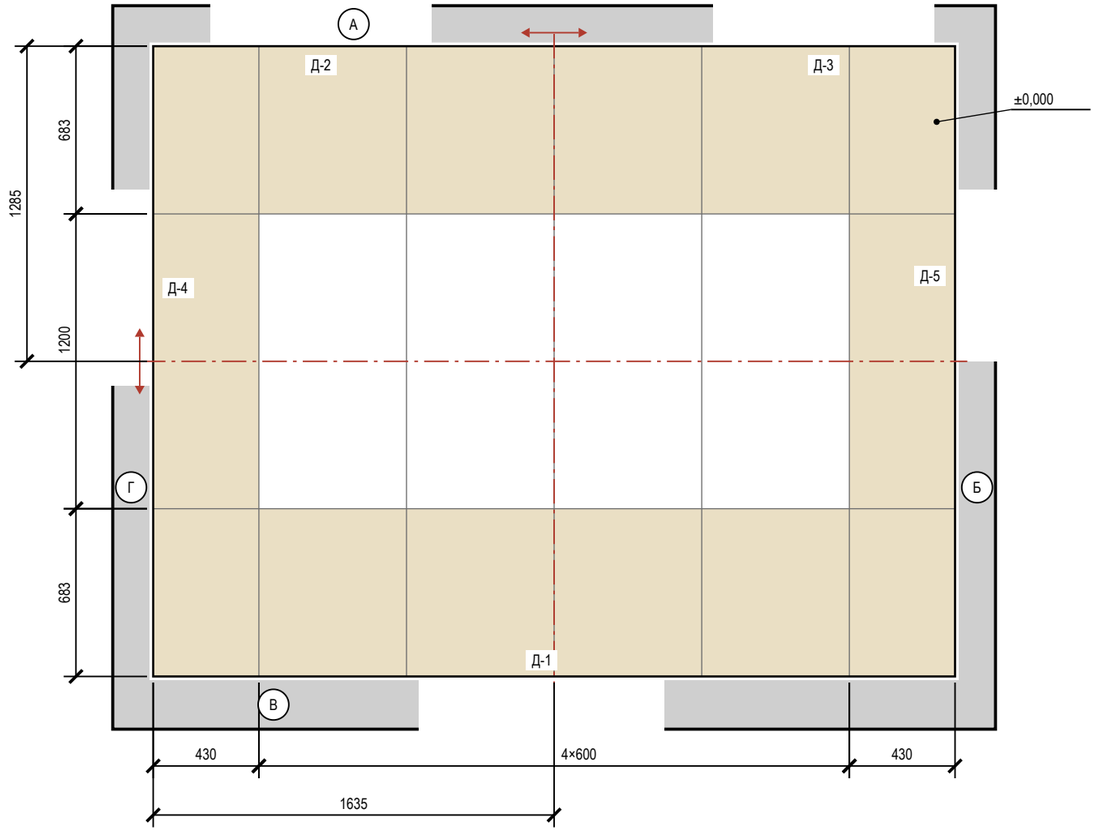

Фрагмент 2. Гостиная-кухня (пом. 1), фартук, стена Г. 1200×600, шов 2 мм, М 1:25

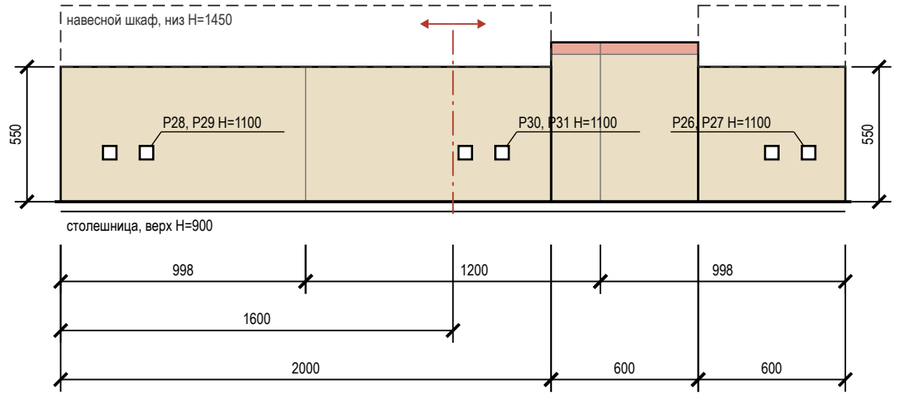

Условные обозначения

- плитка целая; тонкая линия — шов
- плитка с подрезкой (размер — на цепочке)
- ось старта; стрелки — направление укладки
- электроточка: марка и Н — по листам ЭОМ
- столешница (верх)
- навесной шкаф над фартуком
- отметка чистого пола на полке выноски, м
- (А) обозначение стены А–Г (как на развёртках)

Подсчёт плитки

Поверхность	Формат	S, м²	Целых	Подр.	С запасом
Прихожая, пол	600×1200	8,58	4	14	20
Гостиная-кухня, фартук (ст. Г)	1200×600	1,82	0	5	6

Сдвиг розеток фартука под раскладку

Точка (ЭОМ)	Проект: от угла / Н	Под раскладку: от угла / Н	Сдвиг, мм
Р26, Р27, Р30, Р31	3050, 2900, 1800, 1650 / 1100	3050, 2900, 1800, 1650 / 1175	Н +75 — ось ряда
Р28, Р29	350, 200 / 1100	350, 200 / 1175	Н +75 — ось ряда

Примечания

1. Прихожая: керамогранит 600×1200, длинная сторона — вдоль стен Б и Г, шов 2 мм, прямая раскладка от центра. Стены окрашены: раскладка от чистового контура минус штукатурка и шпаклёвка 15 мм на сторону (принято); подрезки 430 / 683 мм, срез — под плинтус.
2. Прихожая: деформационный зазор по периметру 8–10 мм под плинтусом; в проёмах — стык с соседним покрытием по оси полотна двери. Клей С2 TE S1, затирка CG2WA.
3. Фартук, Гостиная-кухня: 1200×600 горизонтально, шов 2 мм; зоны 600 мм — 900…1450, 600 мм — 900…1550, 2000 мм — 900…1450 (от столешницы до низа навесного шкафа, без шкафа — 650 мм). Старт от центра участка, подрезки 998 мм. Площадь 1,82 м² — как в ведомости отделки.
4. Фартук — после монтажа столешницы, низ на 2–3 мм выше неё, шов со столешницей — санитарный герметик; навесные шкафы — после фартука. Торцы у пенала и стены — профиль или запил 45°.
5. Фартук, Гостиная-кухня: в зоне до отм. 1550 верхний ряд подрезан 48 мм — меньше 1/3 плитки; полоса прикрыта корпусом навесного модуля и на виду не остаётся. Раскладкой не снимается: убрать подрезку можно, только выровняв низ этого модуля с соседними (1450 мм) — решение мебельщика.
6. Розетки из таблицы переносятся до черновой электрики: по высоте — на ось ряда плитки, от вертикального шва крупной плитки — не ближе 60 мм. Привязка — от левого края фартука на развёртке.
7. Клей, затирка и итог по форматам — в ведомостях листа «Раскладка плитки. Планы полов».

Допущения и предложения на листе

Основа листа: размеры помещений и положение проёмов введены заказчиком в брифе, на объекте не замерены (К-1); высота потолка 2700 мм — по брифу заказчика, не замерена (К-2); толщины стен приняты по брифу: наружные 200 мм, внутренние 150 мм — не обмерены (К-1); тип дома монолитный, перекрытие 200 мм — по брифу заказчика, документов нет (К-3); планировка (стены, проёмы, объединение кухни и гостиной, расширение санузла) — по брифу без обмера и плана БТИ (К-7); разрешённая мощность 10 кВт принята, ТУ не переданы (К-8); вентканалы приняты, в брифе не заданы (К-9); подрайон климата не задан — принят не северный (жилые от 2,5 м) (К-10).
Знак «**» — предложение проектировщика, заказчиком не утверждено (согласовать с заказчиком): записи в реестре нет: плинтус пом. 1, 5, фартук пом. 1 — артикул изделия не выбран: позиция описана характеристиками («аналог по характеристикам»), артикул выбирается при закупке.
См. лист открытых вопросов (лист 5, записи К-1–К-3, К-7–К-10).

1000 мм · печать 1:1

Изм.	Кол.уч	Лист	№ док.	Подп.	Дата
Разраб.		Кырлан А.С.			21.10.26
Пров.					
ГИП					
Н. контр.					
Утв.					

ГД-2026-011-АИ

Квартира 56 м²

ЖК «Северный парк», Москва

Дизайн-проект интерьера

Стадия	Лист	Листов
РП	41	83

Раскладка плитки. Прихожая. Фартук кухни


М 1:25

Кырлан Александр Сергеевич

выпуск 19.10.2026 № 1c3e34763b · стр. 49 из 117

Раскладка плитки. Санузел. Развёртки стен

Пом. 4 · вид изнутри помещения · размеры в мм · высоты от чистого пола, отметки от ±0,000

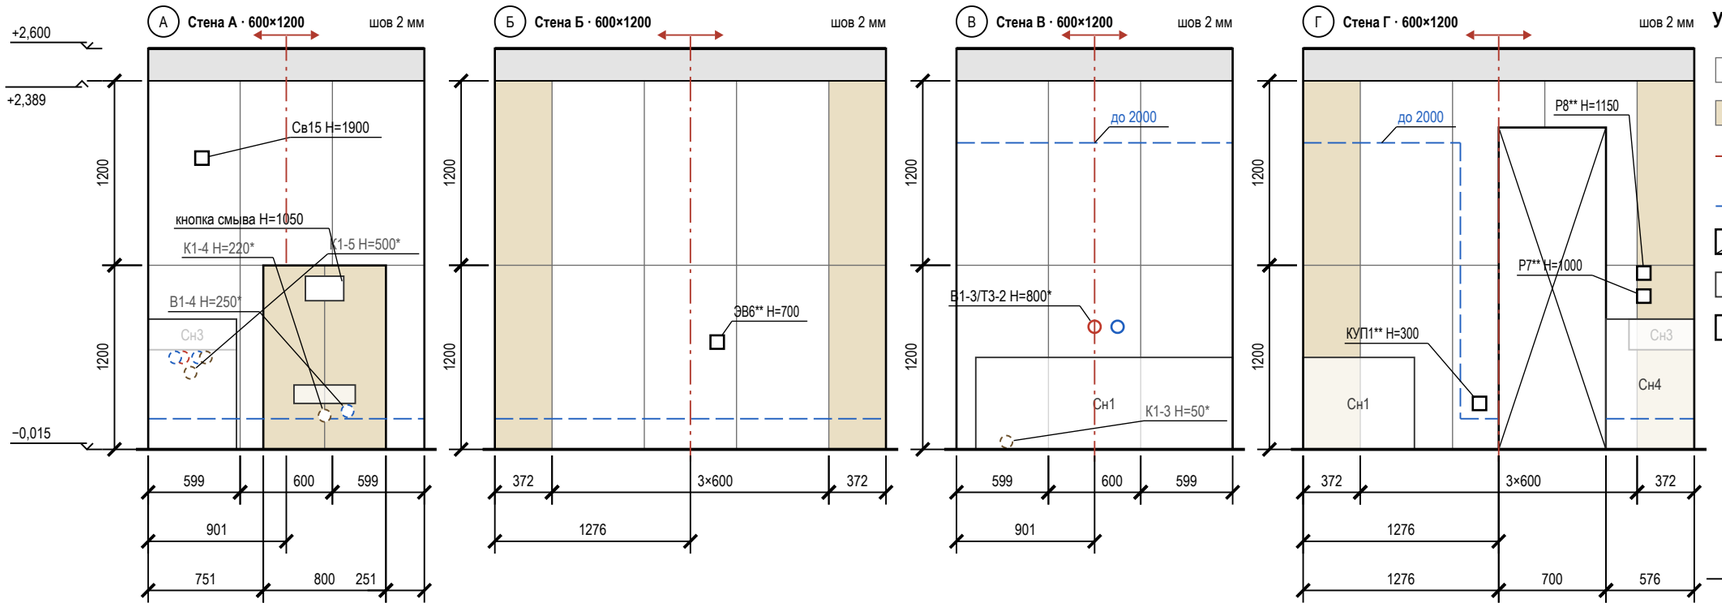

Условные обозначения

- плитка целая; тонкая линия — шов
- плитка с подрезкой (размер — на цепочке)
- ось старта; стрелки — направление укладки
- верх гидроизоляции: 200 от ЧП, в мокрой зоне — «до …»
- проём — не облицовывается
- сантехприбор: габарит, высота по практике
- короб инсталляции, в нём кнопка смыва 250×160
- вывод В1 (код — в ведомости привязок)
- вывод Т3 (код — в ведомости привязок)
- вывод К1 (код — в ведомости привязок)
- вывод за прибором / в коробе (не на сетке)
- электроточка: марка и Н — по листам ЭОМ
- отметка уровня, м: ±0,000 — чистый пол жилых помещений
- низ потолка; серая полоса — стена без плитки
- А — обозначение стены А–Г (как на развёртках)

Подсчёт плитки по стенам и коробу

Поверхность	L × H, мм	S, м²	Целых	Подр.	С запасом	Подрезки: край / верх, мм
стена А	1802 × 2404	3,49	4	2	7	599 / 599; целый ряд
короб (ст. А)	800×1200×250	1,76	0	6	7	лицо 399 / 399; бок. 250
стена Б	2552 × 2404	6,25	6	4	11	372 / 372; целый ряд
стена В	1802 × 2404	4,45	6	0	7	599 / 599; целый ряд
стена Г	2552 × 2404	4,78	2	8	11	372 / 372; целый ряд
Итого		**20,73**	**18**	**20**	**43**	

Сдвиг точек под раскладку

Точка (ВК, ЭОМ)	Стена	Проект: от угла / Н	Под раскладку: от угла / Н	Сдвиг, мм
Св15	А	351 / 1900	299 / 1900	−52 в центр плитки
ЭВ6**	Б	1451 / 700	1577 / 700	+126 на шов
В1-3/Т3-2	В	976 / 800	901 / 800	−75 в центр плитки
Р7**, Р8**	Г	2223 / 1000, 1150	2179 / 1000, 1150	−44 на шов
КУП1**	Г	1151 / 300	1276 / 300	+125 в центр плитки

Примечания

1. Вид изнутри, стены по часовой стрелке А → Г. Высоты — от чистого пола (−0,015), отметки — от ±0,000. Раскладка от чистовых размеров (штукатурка 10 + клей 5 + плитка 9 мм), подрезки чистые; старт — от оси стены, ряды от пола целыми.
2. Верх плитки +2,389, потолок +2,600, зазор 211 мм: потолок ГКЛ опустить до +2,392 (шов 3 мм, герметик) — согласовать с монтажником ГКЛ; иначе профиль-окантовка, полосу окрасить в цвет потолка. Подрезной ряд 206 мм не делать.
3. Точки из таблицы сдвигов переносятся до черновой разводки: смеситель — по оси пары В1 + Т3; вывод на оси прибора — вместе с прибором, иначе старт раскладки — на ось прибора.
4. Выводы — по «Плану выводов сантехники», электроточки — по ЭОМ, «*» — высота по практике; за приборами и в коробе (В1-4, К1-4, Т3-3/В1-5, К1-5, В1-6, К1-6, К1-3) — штриховым кольцом.
5. Гидроизоляция: 200 мм от ЧП по периметру; над ванной — до 2000 и 300 мм за борт (СП 29.13330.2011, п. 7.2 — на высоту замачивания); углы — лентой; акт скрытых работ, пролив.
6. Короб 800×1200×250: лицо 399 / 399 мм от оси кнопки смыва, боковины, полка; углы — запил 45° или профиль; за коробом плитку не кладут.

Допущения и предложения на листе

Основа листа: размеры помещений и положение проёмов введены заказчиком в брифе, на объекте не замерены (К-1); высота потолка 2700 мм — по брифу заказчика, не замерена (К-2); толщины стен приняты по брифу: наружные 200 мм, внутренние 150 мм — не обмерены (К-1); тип дома монолитный, перекрытие 200 мм — по брифу заказчика, документов нет (К-3); планировка (стены, проёмы, объединение кухни и гостиной, расширение санузла) — по брифу без обмера и плана БТИ (К-7); разрешённая мощность 10 кВт принята, ТУ не переданы (К-8); вентканалы приняты, в брифе не заданы (К-9); подрайон климата не задан — принят не северный (жилые от 2,5 м) (К-10).

Знак «**» — предложение проектировщика, заказчиком не утверждено (согласовать с заказчиком): К-5: дверь пом. 4 (стена Г) — дверь в новой перегородке: проём по брифу, короб скрытой двери и размер в свету — после выбора модели и утверждения перегородки (К-5); записи в реестре нет: Р7, Р8 — по образцу: Р7, Р8 и Р33 на высоте 1000 мм — верхний предел нормы (ПУЭ, п. 6.6.30, не выше 1 м); флаг решения снят; КУП1 — по образцу: Добавлены выводы к вентиляторам: ЭВ4 (ВР1, ванная) и ЭВ5 (ВР3, санузел 2) — группа 3, высота 2389 мм, включение с основным светом, таймер выбега в вентиляторе; и коробки уравнивания потенциалов КУП1 (ванная) и КУП2 (санузел 2) — высота 300 мм, у входа, вне зон 0–2, проводник от шины РЕ щита ЩК, сече; ЭВ6 — по образцу: Добавлены электрические полотенцесушители IP44: П10 в ванной (480 мм, низ 900 мм) и П13 в санузле 2 (400 мм, низ 900 мм), выводы ЭВ6 и ЭВ7; мощность группы 13 — 2,4 кВт вместо 1,8 кВт.

См. лист открытых вопросов (лист 5, записи К-1–К-3, К-5, К-7–К-10).

1000 мм · печать 1:1

Изм.	Кол.уч	Лист	№ док.	Подп.	Дата	ГД-2026-011-АИ			
						Квартира 56 м² ЖК «Северный парк», Москва			
Разраб.		Кырлан А.С.			21.10.26	Дизайн-проект интерьера	Стадия	Лист	Листов
Пров.							РП	42	83
ГИП									
						Раскладка плитки. Санузел. Развёртки стен	**Кырлан Александр Сергеевич**		
Н. контр.						М 1:40			
Утв.									

выпуск 19.10.2026 № 1c3e34763b · стр. 50 из 117

07

Полы и отделка

Кырлан Александр Сергеевич

выпуск 19.10.2026 № 1c3e34763b · стр. 51 из 117


План полов

Покрытия, направление укладки, отметки чистого пола, стыки · размеры в мм · отметки в м

ПРЕДВАРИТЕЛЬНО · не для производства работ · открыто пунктов: 10 (реестр — л. 5)

Условные обозначения

- тип 1 — инженерная доска, линии — вдоль доски
- тип 2 — керамогранит 600×1200, сетка — формат плитки
- тип 3 — керамогранит 600×1200, сетка — формат плитки
- 1 — номер типа пола (экспликация полов)
- схема пола, без масштаба: плита — штриховка, стяжка — точки, звукоизоляция — зигзаг, гидроизоляция — утолщённая линия с заведением на стену
- направление укладки (длинная сторона доски)
- отметка чистого пола, м
- стык в проёме: Т-профиль по оси полотна
- стык в проёме: порог
- СТ1 — марка стыка (ведомость стыков)
- стояк: К1 — канализация, В1 ХВС, Т3 — ГВС
- новое — возводится по проекту (синим)
- 1 — номер помещения, площадь м²

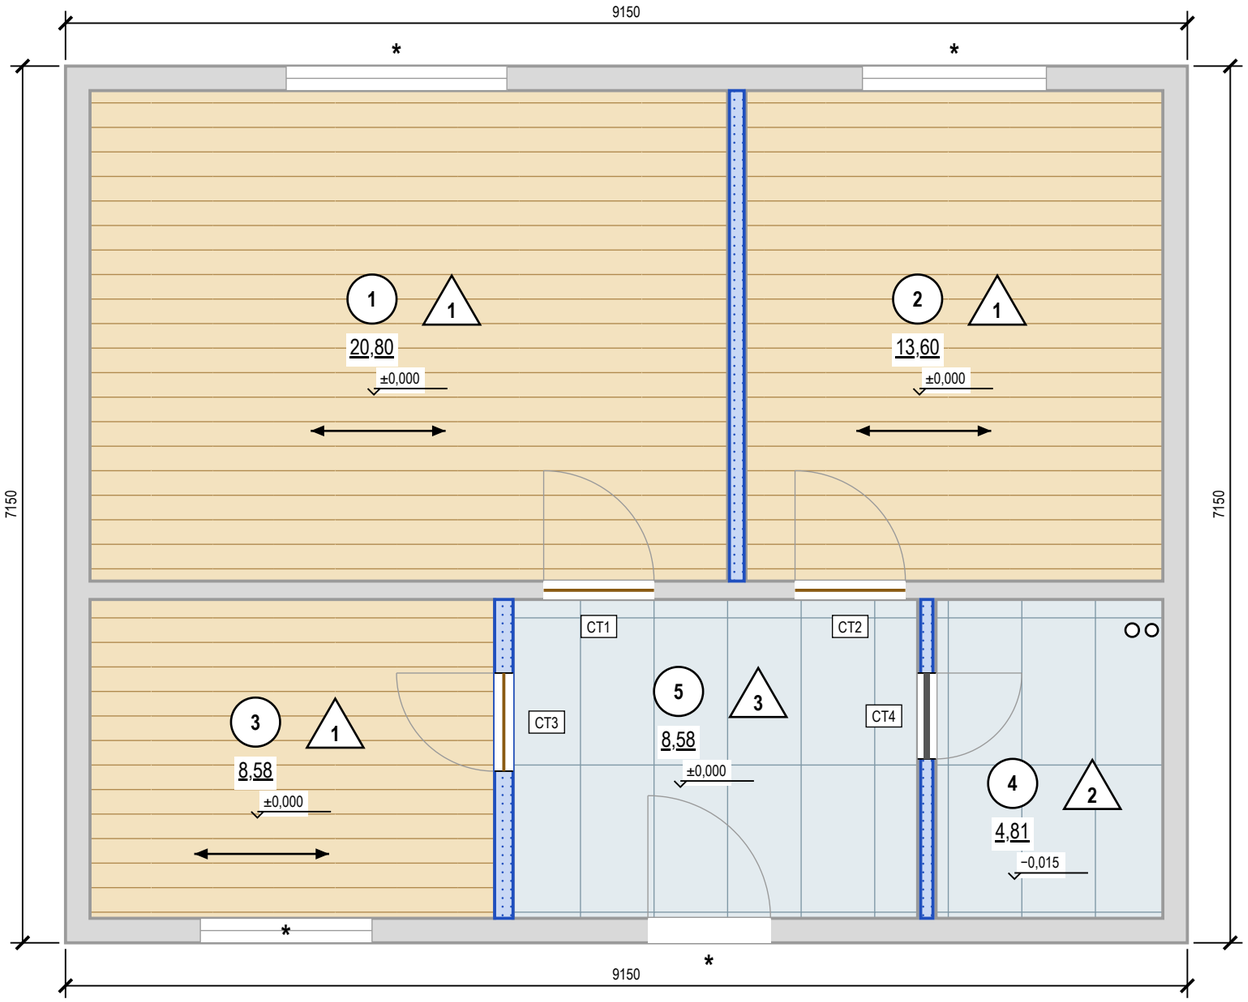

Экспликация полов

Пом.	Тип пола	Схема пола	Элементы пола, толщина, мм	Площадь, м²
1, 2, 3	1		Инженерная доска на клею — 14 Стяжка ЦПС М200 50 Плита перекрытия Всего 64 мм; ЧП ±0,000, верх плиты −0,064	42,98
4	2		Керамогранит на клею С2 TE S1 — 14 Гидроизоляция обмазочная, 2 слоя, с заведением на стены 200 мм — 2 Стяжка ЦПС М200 33 Плита перекрытия Всего 49 мм; ЧП −0,015, верх плиты −0,064	4,81
5	3		Керамогранит на клею С2 TE S1 — 14 Стяжка ЦПС М200 50 Плита перекрытия Всего 64 мм; ЧП ±0,000, верх плиты −0,064	8,58
			Итого	**56,37**

Стыки покрытий в проёмах

Марка	Проём	Типы пола	Отметки ЧП	Решение
СТ1	1–5 (Д-2)	1 / 3	±0,000 / ±0,000	Т-профиль
СТ2	2–5 (Д-3)	1 / 3	±0,000 / ±0,000	Т-профиль
СТ3	3–5 (Д-4)	1 / 3	±0,000 / ±0,000	Т-профиль
СТ4	4–5 (Д-5)	2 / 3	−0,015 / ±0,000	порог h=15 мм

Допущения и предложения на листе. Знак «*» принято (замерить): дверь пом. 1 (стена В), 2 (В), Ст К1-1, Ст В1-1. Знак «**» предложено (согласовать): плинтус пом. 1, 2, 5, фартук пом. 1, дверь пом. 3 (стена Б), 4 (Г), П-1, П-2, П-3. См. лист открытых вопросов (лист 5).

Отметки по высоте

±0,000	чистый пол пом. 1–3, 5; отсчёт высот
−0,015	чистый пол пом. 4, ниже на 15 мм
−0,064*	верх плиты — расчёт, не замер (задание на обмер)
сущ. пол	снимается до плиты; не замерен (задание на обмер)

Примечания

1. За отметку ±0,000 принят чистый пол, не существующий (блок отметок). Площади — по чистым размерам помещений, м²; размеры — в мм.
2. Стык разнотипных покрытий — по оси дверного полотна (под полотном в закрытом положении); решение стыка — по ведомости стыков.
3. Пол санузлов ниже смежных помещений на 15 мм за счёт меньшей толщины стяжки (верх плиты общий — по экспликации полов); гидроизоляция по стяжке с заведением на стены не менее 200 мм (СП 29.13330.2011, п. 7.2), до облицовки — тест проливом и акт скрытых работ.
4. Трубопроводы в конструкции пола не прокладываются: пирог пола 49–64 мм не вмещает выпуски канализации с уклоном — выпуски К1 ведутся по стенам над чистым полом в коробах (лист 32).
5. Звукоизоляционный слой под стяжкой проектом не предусмотрен (стяжка по плите): приведённый уровень ударного шума перекрытия с полом Lnw не более 60 дБ (СП 51.13330.2011, табл. 2) подтвердить по данным дома; при превышении — плавающая стяжка по звукоизоляции с демпферной лентой по контуру и у стояков, пирог пересчитать.
6. Штучные покрытия (инженерная доска): направление — по стрелке; влажность основания по СМ не более 2,0 % (по ТУ изготовителя).
7. Ровность основания — просвет под 2-метровой рейкой не более 2 мм: пом. 1, 2, 3 (инженерная доска), пом. 4, 5 (керамогранит); проверить до укладки покрытия (СП 71.13330.2017, табл. 8.5).
8. Сетка на плитке — условная, в размер формата; точка старта и раскладка — по листу раскладки плитки.
9. Узор покрытия (заливка-код типа пола) прерывается под надписями — площадями помещений и отметками чистого пола.
10. Пироги полов — по экспликации полов: слои сверху вниз, толщины в мм; гидроизоляция мокрых зон — в пироге и в ведомости отделки; схема пола — без масштаба.

1000 мм · печать 1:1

Изм.	Кол.уч	Лист	№ док.	Подп.	Дата
Разраб.		Кырлан А.С.			21.10.26
Пров.					
ГИП					
Н. контр.					
Утв.					

ГД-2026-011-АИ

Квартира 56 м²

ЖК «Северный парк», Москва

Дизайн-проект интерьера

Стадия	Лист	Листов
РП	43	83

План полов

М 1:50

Кырлан Александр Сергеевич

выпуск 19.10.2026 № 1c3e34763b · стр. 52 из 117

Ведомость отделки помещений

Потолки, стены, низ стен, полы · площади в м², длины в м · отметки в м

Ведомость отделки помещений (форма 1 прил. А ГОСТ 21.501-2018)

№	Наименование помещения	Потолок			Стены и перегородки			Низ стен (плинтус)			Пол		Примечание
		Вид отделки	Код цвета	S, м²	Вид отделки	Код цвета	S, м²	Вид отделки	Код цвета	L, м	Вид отделки	S, м²	
1	Гостиная-кухня 20,80 м²	ГКЛ по каркасу П113, отм. +2,600; +2,500; окраска, Tikkurila Euro Power 7, глубокоматовая, 2 слоя, подготовка Q3	Tikkurila F485	20,80	Окраска, Tikkurila Euro Power 7, колеровка по NCS, матовая, 2 слоя, подготовка Q3 Акцент — стена А: окраска, Farrow & Ball Modern Emulsion, матовая, 2 слоя, подготовка Q3 Фартук кухни (стена Г): облицовка керамогранитом, аналог: керамогранит под травертин, матовый, 1200×600×9 мм, клей C2 TE S1, затирка CG2WA	NCS S 0804-Y30R Farrow & Ball No. 298 по артикулу	30,61 10,82 1,82	Плинтус МДФ h=80 мм, аналог: МДФ под покраску 80×16	NCS S 0804-Y30R	17,5	Инженерная доска, 1167-1101, 2100×127 мм, на клею; тип 1, отм. ЧП ±0,000	20,80	Н стен 2600 (до потолка); матовая моющаяся, класс 1 EN 13300 — осознанно вместо полуматовой; плинтус в цвет: стены
2	Спальня 13,60 м²	ГКЛ по каркасу П113, отм. +2,500; +2,600; окраска, Tikkurila Euro Power 7, глубокоматовая, 2 слоя, подготовка Q3	Tikkurila F485	13,60	Окраска, Tikkurila Euro Power 7, колеровка по NCS, матовая, 2 слоя, подготовка Q3 Акцент — стена А: окраска, Tikkurila Euro Power 7, колеровка по NCS, матовая, 2 слоя, подготовка Q3	NCS S 0804-Y30R NCS S 5010-G70Y	26,61 6,33	Плинтус МДФ h=80 мм, аналог: МДФ под покраску 80×16	NCS S 0804-Y30R	13,9	Инженерная доска, 1167-1101, 2100×127 мм, на клею; тип 1, отм. ЧП ±0,000	13,60	Н стен 2500 (до потолка); плинтус в цвет: стены
3	Детская 8,58 м²	ГКЛ по каркасу П113, отм. +2,500; +2,600; окраска, Tikkurila Euro Power 7, глубокоматовая, 2 слоя, подготовка Q3	Tikkurila F485	8,58	Окраска, Tikkurila Euro Power 7, колеровка по NCS, матовая, 2 слоя, подготовка Q3 Акцент — стена Г: окраска, Tikkurila Euro Power 7, матовая, 2 слоя, подготовка Q3	NCS S 0804-Y30R Tikkurila X447	19,29 6,50	Плинтус МДФ h=69 мм, SX165	NCS S 0804-Y30R	11,0	Инженерная доска, 1167-1101, 2100×127 мм, на клею; тип 1, отм. ЧП ±0,000	8,58	Н стен 2500 (до потолка); плинтус в цвет: стены
4	Санузел 4,81 м²	ГКЛВ по каркасу П113, отм. +2,600; окраска, Tikkurila Euro Power 7, матовая, 2 слоя, подготовка Q3	Tikkurila F485	4,81	Облицовка плиткой, A8UZ, 600×1200×9 мм, клей C2 TE S1, затирка CG2WA	Atlas Concorde A8UZ	19,93	нет			Керамогранит, A8UZ, 600×1200×9 мм; тип 2, отм. ЧП −0,015	4,81	Н стен 2615 (до потолка); гидроизоляция обмазочная, 2 слоя, с заведением на стены 200 мм (по пирогу пола); тест проливом и акт скрытых работ
5	Прихожая 8,58 м²	ГКЛ по каркасу П113, отм. +2,600; окраска, Tikkurila Euro Power 7, глубокоматовая, 2 слоя, подготовка Q3	Tikkurila F485	8,58	Окраска, Tikkurila Euro Power 7, колеровка по NCS, матовая, 2 слоя, подготовка Q3	NCS S 0804-Y30R	21,65	Плинтус МДФ h=80 мм, аналог: МДФ под покраску 80×16	NCS S 0804-Y30R	7,5	Керамогранит, A8UZ, 600×1200×9 мм; тип 3, отм. ЧП ±0,000	8,58	Н стен 2600 (до потолка); матовая моющаяся, класс 1 EN 13300 — осознанно вместо полуматовой; плинтус в цвет: стены
	Итого			**56,37**			**143,55**			**49,9**		**56,37**	

Допущения и предложения на листе

Основа листа: размеры помещений и положение проёмов введены заказчиком в брифе, на объекте не замерены (К-1); высота потолка 2700 мм — по брифу заказчика, не замерена (К-2); толщины стен приняты по брифу: наружные 200 мм, внутренние 150 мм — не обмерены (К-1); тип дома монолитный, перекрытие 200 мм — по брифу заказчика, документов нет (К-3); планировка (стены, проёмы, объединение кухни и гостиной, расширение санузла) — по брифу без обмера и плана БТИ (К-7); разрешённая мощность 10 кВт принята, ТУ не переданы (К-8); вентканалы приняты, в брифе не заданы (К-9); подрайон климата не задан — принят не северный (жилые от 2,5 м) (К-10).

Знак «**» — предложение проектировщика, заказчиком не утверждено (согласовать с заказчиком): записи в реестре нет: плинтус пом. 1, 2, 5, фартук пом. 1 — артикул изделия не выбран: позиция описана характеристиками («аналог по характеристикам»), артикул выбирается при закупке.

См. лист открытых вопросов (лист 5, записи К-1–К-3, К-7–К-10).

Примечания

1. Площади поверхностей — по чистым граням стен до отделки: стены = периметр × высоту от чистого пола помещения до низа потолка минус проёмы (облицовка плиткой — до верха облицовки); плинтус = периметр минус дверные проёмы; пол и потолок — по площади помещения. Количество плиток по раскладке. Площади помещений — с учётом всех частей помещения; откосы в площадь стен не входят.
2. Акцентные стены и фартук — отдельными строками, их площадь вычтена из основной отделки стен помещения; фартук — над нижними модулями кухни от столешницы до низа навесных шкафов, где шкафов нет — на 600 мм.
3. Плинтус — длина по периметру за вычетом дверных проёмов; примыкания к наличникам и встроенной мебели — по развёрткам.
4. Формат плитки — Ш×В×Т (ширина × высота в положении укладки × толщина), мм; на полу — вдоль стен А/В × вдоль стен Б/Г.
5. Коды цвета — по веерам производителей; колеровка каждой краски одной партией, проверка выкраса при свете D65 и при лампах проекта.
6. Уровни подготовки Q1–Q4 — система Knauf, не норма ГОСТ/СП; допуски поверхностей — по СП 71.13330.2017 (действующая редакция).
7. «аналог:» — изделие задано характеристиками, марку и артикул согласовать с заказчиком до закупки.
8. Сводка площадей по материалам, м²: потолок — Tikkurila F485 Euro Power 7 — 56,37; стены — NCS S 0804-Y30R Euro Power 7, колеровка по NCS 98,16; стены — Farrow & Ball No. 298 Modern Emulsion — 10,82; стены — NCS S 5010-G70Y Euro Power 7, колеровка по NCS — 6,33; стены — Tikkurila X447 Euro Power 7 — 6,50; стены — облицовка плиткой 600×1200×9 мм, Atlas Concorde A8UZ — 19,93; фартук — облицовка керамогранитом 1200×600×9 мм — 1,82.

Изм.	Кол.уч	Лист	№ док.	Подп.	Дата
Разраб.		Кырлан А.С.			21.10.26
Пров.					
ГИП					
Н. контр.					
Утв.					

ГД-2026-011-АИ

Квартира 56 м²

ЖК «Северный парк», Москва

Дизайн-проект интерьера

Стадия	Лист	Листов
РП	44	83

Ведомость отделки помещений

М б/м

Кырлан Александр Сергеевич

Колерная карта

Цвета и материалы по помещениям · палитра проекта · выкрасы на согласование

Колерная карта по помещениям

Помещение	Поверхность	Образец	Поз.	Система и код цвета	Производитель, линейка / материал, артикул	Блеск	Класс EN 13300	LRV	Площадь
1. Гостиная-кухня 20,8 м²	стены		**К1**	NCS S 0804-Y30R	Tikkurila · Euro Power 7, колеровка по NCS	матовая	1	78	30,6 м²
	акцент А		**К2**	Farrow & Ball No. 298	Farrow & Ball · Modern Emulsion	матовая	1	≈14	10,8 м²
	потолок		**К3**	Tikkurila F485	Tikkurila · Euro Power 7	глубокомат.	2	83	20,8 м²
	пол		**КМ1**	по образцу	Coswick · Классическая				20,8 м²
	плинтус		**К4**	NCS S 0804-Y30R	МДФ · в цвет NCS			78	17,5 м
	фартук		**КМ2**	по образцу	керамогранит · аналог по хар.				1,8 м²
2. Спальня 13,6 м²	стены		**К1**	NCS S 0804-Y30R	Tikkurila · Euro Power 7, колеровка по NCS	матовая	1	78	26,6 м²
	акцент А		**К5**	NCS S 5010-G70Y	Tikkurila · Euro Power 7, колеровка по NCS	матовая	1	22	6,3 м²
	потолок		**К3**	Tikkurila F485	Tikkurila · Euro Power 7	глубокомат.	2	83	13,6 м²
	пол		**КМ1**	по образцу	Coswick · Классическая				13,6 м²
	плинтус		**К4**	NCS S 0804-Y30R	МДФ · в цвет NCS			78	13,9 м
3. Детская 8,58 м²	стены		**К1**	NCS S 0804-Y30R	Tikkurila · Euro Power 7, колеровка по NCS	матовая	1	78	19,3 м²
	акцент Г		**К6**	Tikkurila X447	Tikkurila · Euro Power 7	матовая	1	63	6,5 м²
	потолок		**К3**	Tikkurila F485	Tikkurila · Euro Power 7	глубокомат.	2	83	8,6 м²
	пол		**КМ1**	по образцу	Coswick · Классическая				8,6 м²
	плинтус		**К7**	NCS S 0804-Y30R	Orac Decor · Contour (Luxxus)			78	11,0 м
4. Санузел 4,81 м²	стены		**К8**	Atlas Concorde A8UZ	Atlas Concorde · Marvel Travertine				19,9 м²
	потолок		**К9**	Tikkurila F485	Tikkurila · Euro Power 7	матовая	1	83	4,8 м²
	пол		**К8**	Atlas Concorde A8UZ	Atlas Concorde · Marvel Travertine				4,8 м²
5. Прихожая 8,58 м²	стены		**К1**	NCS S 0804-Y30R	Tikkurila · Euro Power 7, колеровка по NCS	матовая	1	78	21,6 м²
	потолок		**К3**	Tikkurila F485	Tikkurila · Euro Power 7	глубокомат.	2	83	8,6 м²
	пол		**К8**	Atlas Concorde A8UZ	Atlas Concorde · Marvel Travertine				8,6 м²
	плинтус		**К4**	NCS S 0804-Y30R	МДФ · в цвет NCS			78	7,5 м

Перечень выкрасов на согласование

№	Код	Бренд / веер	Пом. / стена	Подложка	Формат	Статус
1	S 0804-Y30R	NCS Tikkurila	1, 2, 3, 5	ГКЛ, загрунтованный под эту краску; МДФ, загрунтованный под эмаль	600×1000; 300×600	к выполнению
2	No. 298	Farrow & Ball	1 А	ГКЛ, загрунтованный под эту краску	600×1000	к выполнению
3	F485	Tikkurila	1, 2, 3, 4, 5	ГКЛ, загрунтованный под эту краску	600×1000	к выполнению
4	S 5010-G70Y	NCS Tikkurila	2 А	ГКЛ, загрунтованный под эту краску	600×1000	к выполнению
5	X447	Tikkurila	3 Г	ГКЛ, загрунтованный под эту краску	600×1000	к выполнению

Примечания

1. Цвет утверждается только по выкрасу на объекте: формат от А3 до 1000×1000 мм на загрунтованном ГКЛ, в 2 слоя (как на стене), не на белой шпаклёвке; смотреть днём и при свете проекта своего помещения, рядом с образцами пола и фасадов. Подпись на обороте: код, бренд и веер, дата.
2. Колеровка машинная в колеровочном центре бренда; каждый код — за один проход, одной партией на весь объём. Колеровщику передаётся только система и код утверждённого веера; плашки и HEX на листе — ориентир, печать не является эталоном цвета.
3. Класс мокрого истирания — EN 13300 (ISO 11998); блеск — по ГОСТ 31975 (ISO 2813), геометрия 60°. LRV — пересчёт координаты L* каталога производителя (Y = ((L*+16)/116)³); «≈» — расчёт по HEX, справочно.
4. Площади поверхностей — тем же способом и с теми же цифрами, что в ведомости отделки (способ счёта — в общих указаниях); объём краски к заказу, фасовка и материалы КМ — в спецификации отделочных материалов.
5. Перечень выкрасов составлен по кодам колерной карты; к основному тону стен добавить на выкрас 2 соседних тона того же веера (светлее и темнее), статус отмечать в графе «Статус» при согласовании.
6. Узор штриховки сегмента «без кода цвета» на полосах 60/30/10 прерывается под числами долей (белая подложка), границы сегментов не прерываются.

Допущения и предложения на листе. Знак «**» предложено (согласовать): плинтус пом. 1, 2, 5, фартук пом. 1. См. лист открытых вопросов (лист 5).

Схема квартиры: цвет стен и акценты (б/м)

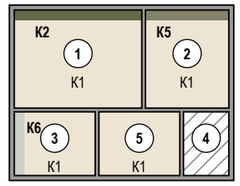


Схема палитры проекта


Стиль: Джапанди · схема: аналоговая

основной	основной	основной	второстепенный	второстепенный	второстепенный	акцентный	акцентный	акцентный
NCS S 0804-Y30R	**Tikkurila F485**	**Little Greene No. 105**	**Tikkurila X447**	**Tikkurila V484**	**NCS S 2005-Y30R**	**Farrow & Ball No. 298**	**NCS S 5010-G70Y**	**NCS S 7005-Y20R**
светлый «рисовая бумага» LRV 78 стены 1,2,3,5; плинтус 1,2,3,5	Damask LRV 83 потолок 1,2,3,4,5; текстиль/декор 1,2,3	Slaked Lime LRV 82 в отделке не применён	Sea Smoke LRV 63 акцент 3; текстиль/декор 1,2,3	Driftwood LRV 47 текстиль/декор 1,3	песочный грейж LRV 55 текстиль/декор 2	Bancha LRV ≈14 акцент 1; текстиль/декор 1	приглушённая олива LRV 22 акцент 2; текстиль/декор 2	тёмный орех LRV 9 в отделке не применён

План 60/30/10



Окраска, факт — по площади стен, акцентов, потолков

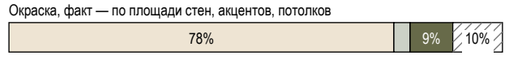

окрашено всего 198,1 м²; второстепенный тон несут мебель и текстиль

Текстиль и декор в цветах вне палитры проекта

NCS S 1002-Y50R тёплый светлый грейж — пом. 3 (Т10)

Условные обозначения

- **К1** NCS S 0804-Y30R · светлый «рисовая бумага» · Tikkurila Euro Power 7, колеровка по NCS · матовая · кл. 1
- **К2** Farrow & Ball No. 298 · Bancha · Modern Emulsion · матовая · кл. 1
- **К3** Tikkurila F485 · Damask · Euro Power 7 · глубокомат. · кл. 2
- **К4** NCS S 0804-Y30R · светлый «рисовая бумага» · МДФ
- **К5** NCS S 5010-G70Y · приглушённая олива · Tikkurila Euro Power 7, колеровка по NCS · матовая · кл. 1
- **К6** Tikkurila X447 · Sea Smoke · Euro Power 7 · матовая · кл. 1
- дерево (доска, паркет, ламинат) — рисунок досок
- керамогранит, плитка, камень — сетка швов по формату
- HEX не задан — цвет только по коду и вееру
- **К7** NCS S 0804-Y30R · светлый «рисовая бумага» · Orac Decor Contour (Luxxus)
- **К8** Atlas Concorde A8UZ · Marvel Travertine · Marvel Travertine
- **К9** Tikkurila F485 · Damask · Euro Power 7 · матовая · кл. 1
- **КМ1** инженерная доска · 1167-1101
- **КМ2** аналог: керамогранит под травертин, матовый, 1200×600×9 мм

К — позиция окраски (код + продукт + блеск), КМ — позиция материала, тон КМ — по описанию артикула, эталон — образец материала; ≈ LRV — расчёт по HEX, справочно

Изм.	Кол.уч	Лист	№ док.	Подп.	Дата
Разраб.		Кырлан А.С.			21.10.26
Пров.					
ГИП					
Н. контр.					
Утв.					

ГД-2026-011-АИ

Квартира 56 м²

ЖК «Северный парк», Москва

Дизайн-проект интерьера

Стадия	Лист	Листов
РП	45	83

Колерная карта

М б/м

Кырлан Александр Сергеевич

выпуск 19.10.2026 № 1c3e34763b · стр. 54 из 117

Спецификация отделочных материалов

ПРЕДВАРИТЕЛЬНО · не для производства работ · открыто пунктов: 10 (реестр — л. 5)

Форма 1 по ГОСТ 21.110-2013 · количества — из геометрии проекта, с запасом

Поз.	Наименование и техническая характеристика	Тип, марка, обозначение документа	Код продукции	Поставщик	Ед. изм.	Кол.	Масса 1 ед., кг	Примечание
	Лакокрасочные материалы							
1	Краска интерьерная водно-дисперсионная акриловая для стен, матовая, класс мокрого истирания 1 по EN 13300, база A; цвет NCS S 0804-Y30R «S 0804-Y30R», колеровка машинная	Tikkurila Euro Power 7, колеровка по NCS		Tikkurila	л	27		поз. К1 колерной карты; пом. 1, 2, 3, 5; S = 98,2 м² × 2 сл. × 0,12 л/м² = 23,6 л, +10 % и 0,5 л на подкраску → ≥ 26,4 л; тара 3 × 9 л
2	Краска интерьерная водно-дисперсионная акриловая для акцентных стен, матовая, класс мокрого истирания 1 по EN 13300, база C; цвет Farrow & Ball No. 298 «Bancha», колеровка машинная	Farrow & Ball Modern Emulsion		Farrow & Ball	л	5		поз. К2 колерной карты; пом. 1; S = 10,8 м² × 2 сл. × 0,12 л/м² = 2,6 л, +10 % и 0,5 л на подкраску → ≥ 3,4 л; тара 1 × 5 л
3	Краска интерьерная водно-дисперсионная акриловая для потолков, глубокоматовая, класс мокрого истирания 2 по EN 13300, база A; цвет Tikkurila F485 «Damask», колеровка машинная	Tikkurila Euro Power 7		Tikkurila	л	14,4		поз. К3 колерной карты; пом. 1, 2, 3, 5; S = 51,6 м² × 2 сл. × 0,12 л/м² = 12,4 л, +10 % и 0,5 л на подкраску → ≥ 14,1 л; тара 1 × 9 л + 2 × 2,7 л
4	Краска интерьерная водно-дисперсионная акриловая для акцентных стен, матовая, класс мокрого истирания 1 по EN 13300, база C; цвет NCS S 5010-G70Y «S 5010-G70Y», колеровка машинная	Tikkurila Euro Power 7, колеровка по NCS		Tikkurila	л	2,7		поз. К5 колерной карты; пом. 2; S = 6,3 м² × 2 сл. × 0,12 л/м² = 1,5 л, +10 % и 0,5 л на подкраску → ≥ 2,2 л; тара 1 × 2,7 л
5	Краска интерьерная водно-дисперсионная акриловая для акцентных стен, матовая, класс мокрого истирания 1 по EN 13300, база C; цвет Tikkurila X447 «Sea Smoke», колеровка машинная	Tikkurila Euro Power 7		Tikkurila	л	2,7		поз. К6 колерной карты; пом. 3; S = 6,5 м² × 2 сл. × 0,12 л/м² = 1,6 л, +10 % и 0,5 л на подкраску → ≥ 2,2 л; тара 1 × 2,7 л
6	Краска интерьерная водно-дисперсионная акриловая для потолков, матовая, класс мокрого истирания 1 по EN 13300, база A; цвет Tikkurila F485 «Damask», колеровка машинная	Tikkurila Euro Power 7		Tikkurila	л	1,8		поз. К9 колерной карты; пом. 4; S = 4,8 м² × 2 сл. × 0,12 л/м² = 1,2 л, +10 % и 0,5 л на подкраску → ≥ 1,8 л; тара 2 × 0,9 л
7	Краска для МДФ и дерева в цвет NCS S 0804-Y30R «S 0804-Y30R» — окраска плинтуса; блеск не ниже блеска стен	марка не задана			л	1,3		поз. К4, К7; пом. 1, 2, 3, 5; L = 49,9 м, S = 4,7 м² × 2 сл. × 0,12 л/м² + 10 %; продукт подобрать в веере NCS
8	Грунтовка акриловая под окраску стен и потолков — из системы производителя краски	по системе краски			м²	179		площадь окраски стен, акцентов и потолков; 1 слой перед окраской; расход — по ТУ грунтовки
	Плитка и керамогранит							
9	Керамогранит под травертин, 600×600 мм	аналог по характеристикам			м²	6,12		шов 2 мм; Санузел, пол; по раскладке 15 шт (S = 4,81 м²), с запасом 17 шт
10	Керамогранит под травертин, 600×1200×9 мм, ректификат, водопоглощение 0,1 %	аналог по характеристикам		Atlas Concorde	м²	30,96		шов 2 мм; Санузел, стены А–Г; Санузел, короб инсталляции; по раскладке 38 шт (S = 20,73 м²), с запасом 43 шт
11	A8UZ, 600×1200×9 мм, ректификат, водопоглощение 0,1 % (BIa), противоскольжение R10, PEI IV	A8UZ		Atlas Concorde	м²	14,40		шов 2 мм; Прихожая, пол; по раскладке 18 шт (S = 8,58 м²), с запасом 20 шт
12	Керамогранит под травертин, матовый, 1200×600×9 мм, ректификат, водопоглощение 0,1 % (BIa)	аналог по характеристикам			м²	4,32		шов 2 мм; Гостиная-кухня, фартук (ст. Г); по раскладке 5 шт (S = 1,82 м²), с запасом 6 шт
	Напольные покрытия							
13	1167-1101, рабочий слой 4 мм, эмиссия E1, укладка на клей	1167-1101		Coswick	м²	46		пом. 1, 2, 3; S = 42,98 м² + 7 % (прямая укладка); к заказу — кратно упаковке
14	Клей для паркета и инженерной доски, эластичный (СМП / полиуретановый)	по рекомендации производителя доски			м²	43		площадь приклейки; расход и шпатель — по ТУ клея
	Погонажные изделия							
15	Плинтус МДФ под покраску 80×16, крепление к стене, окраска в цвет NCS S 0804-Y30R	аналог по характеристикам			м	43		пом. 1, 2, 5; L = 38,9 м (периметр без дверных проёмов) + 10 % на подрезку; в штуках — по длине планки
16	SX165, h = 69 мм, крепление к стене, окраска в цвет NCS S 0804-Y30R	SX165		Orac Decor	м	13		пом. 3; L = 11,0 м (периметр без дверных проёмов) + 10 % на подрезку; в штуках — по длине планки
	Смеси и материалы для облицовки							
17	Затирка для швов плитки, класс CG2WA по EN 13888	Mapei Ultracolor Plus 132		Mapei	кг	2,9		по раскладке (a+b)/(a·b) × шов × t × 1,6 + 10 %; в т. ч. 0,8 кг — позиции раскладки без марки
18	Клей плиточный C2 TE S1 по EN 12004, слой 5 мм	Ceresit CM 17		Ceresit	кг	288		12 меш. по 25 кг; 1,5 кг/м² на 1 мм слоя + 10 %; в т. ч. 85 кг — позиции раскладки без марки
19	Гидроизоляция обмазочная мокрых зон: пол, стены по периметру, зоны замачивания; 2 слоя с армирующей лентой в углах	аналог по характеристикам			м²	12,4		площадь по листу раскладки плитки + 10 %; расход смеси — по ТУ
20	Лента демпферная по периметру пола из плитки	аналог по характеристикам			м	16,9		периметр без дверных проёмов + 10 %

Примечания

1. Количества — из геометрии проекта: площади поверхностей по чистым граням стен до отделки (те же, что в ведомости отделки и колерной карте), плитка, клей и затирка — по раскладке плиточника; в графе «Кол.» — к заказу, с запасом.
2. Краска: расход 0,12 л/м² на слой в 2 слоя, если по ТУ не задан иной; запас 10 % и 0,5 л на подкраску каждого кода. Один код — одна партия, колеровка машинная в колеровочном центре бренда; в заказ — только после утверждения выкраса (колерная карта). Фасовка — по каталогу бренда на дату выпуска; к заказу — не меньше расчётного объёма.
3. «Аналог по характеристикам» — допускается изделие другого производителя с характеристиками не ниже указанных, по согласованию с автором проекта.
4. Графы «Код продукции» и «Масса 1 ед.» не заполнены: коды по классификатору продукции не присвоены, масса единицы до 25 кг (ГОСТ 21.110-2013).
5. Грунтовка и клей для доски указаны площадью обработки; объём — по ТУ выбранного продукта.

Допущения и предложения на листе

Основа листа: размеры помещений и положение проёмов введены заказчиком в брифе, на объекте не замерены (К-1); высота потолка 2700 мм — по брифу заказчика, не замерена (К-2); толщины стен приняты по брифу: наружные 200 мм, внутренние 150 мм — не обмерены (К-1); тип дома монолитный, перекрытие 200 мм — по брифу заказчика, документов нет (К-3); планировка (стены, проёмы, объединение кухни и гостиной, расширение санузла) — по брифу без обмера и плана БТИ (К-7); разрешённая мощность 10 кВт принята, ТУ не переданы (К-8); вентканалы приняты, в брифе не заданы (К-9); подрайон климата не задан — принят не северный (жилые от 2,5 м) (К-10).

Знак «**» — предложение проектировщика, заказчиком не утверждено (согласовать с заказчиком): записи в реестре нет: плинтус пом. 1, 2, 5, фартук пом. 1 — артикул изделия не выбран: позиция описана характеристиками («аналог по характеристикам»), артикул выбирается при закупке.

См. лист открытых вопросов (лист 5, записи К-1–К-3, К-7–К-10).

Изм.	Кол.уч	Лист	№ док.	Подп.	Дата
Разраб.		Кырлан А.С.			21.10.26
Пров.					
ГИП					
Н. контр.					
Утв.					

ГД-2026-011-АИ

Квартира 56 м²

ЖК «Северный парк», Москва

Дизайн-проект интерьера

Стадия	Лист	Листов
РП	46	83

Спецификация отделочных материалов

М б/м

Кырлан Александр Сергеевич

выпуск 19.10.2026 № 1c3e34763b · стр. 55 из 117

Концепция декора и визуализации

Джапанди · джапанди · визуализации, палитра, материалы, ключевые предметы



Визуализация 1. Вид сверху (3D): планировка с мебелью, текстилем и декором
Расстановка — по плану мебели (лист 17); шторы, ковры, картины и растения — по плану текстиля и декора (лист 48).



Визуализация 18. Гостиная-кухня (пом. 1)
шторы Т13, Т14 · ковёр Т16 · картина ДК6 · растение ДК7 · подушки, пледы Т17, Т18, Т19



Визуализация 6. Спальня (пом. 2)
шторы Т1, Т2 · ковёр Т3 · картина ДК1 · подушки, пледы Т4, Т5, Т6



Визуализация 14. Детская (пом. 3)
шторы Т7, Т8 · ковёр Т9 · картина ДК3 · зеркало ДК4 · подушки, пледы Т10, Т11, Т12



Визуализация 2. Санузел (пом. 4)
зеркало ДК2

Материалы и фактуры



Дуб натуральный
пол: пом. 1, 2, 3; рамы ДК1, ДК3



Травертин (керамогранит)
пол и стены санузлов, фартук: пом. 1



Букле
подушки: Т10, Т17



Лён
портьеры, подушки: Т1, Т4, Т7, Т13



Бронза и чёрный металл
рамы ДК4, ДК5 — чёрный; фурнитура, светильники — бронза

Ключевые предметы

— Диван Гс2 2000×900 — гостиная-кухня; подушки и плед Т17, Т18, Т19
— Кровати Дт1, Сп1 — над изголовьем картины ДК1, ДК3; текстиль Т4, Т5, Т6, Т10, Т11, Т12
— Ковры Т3, Т9, Т16 — шерсть, на противоскользящей подложке
— Картины ДК1, ДК3, ДК6 — центр на высоте 1200–1550 мм
— Зеркала в рост ДК4; над умывальниками ДК2, ДК5
— Шторы-волна Т1, Т7, Т13 (Tikkurila X447), тюль Т2, Т8, Т14 (Tikkurila F485) — в нишах потолка
— Растение ДК7, ваза ДК8

Настроение

Джапанди по брифу: стены S 0804-Y30R, потолок Damask F485, серо-зелёный Sea Smoke и дуб под маслом, акценты — олива Bancha и тёмный орех; без глянца (К-6). Настроение стиля: тишина, заземлённость, медленная жизнь, тёплый минимализм, ваби-саби, hygge. Свет тёплый, 2200–3000 K.

Примечания

1. Визуализации — образ интерьера. Изделия, размеры, высоты подвеса и привязки — по чертежам (план текстиля и декора — лист 48; шторы и карнизы — лист 49; ведомость текстиля — лист 50; ведомость декора и развеска — лист 51); при расхождении действуют чертежи и ведомости.
2. Коды цвета — ориентир подбора по веерам производителей; ткань утверждается по образцу при дневном свете и при свете проекта 2700–3000 K.
3. Мелкий стайлинг на визуализациях (книги, посуда, свечи) в ведомости не входит и поставляется заказчиком по желанию.

Палитра 60/30/10 и цвета текстиля



- NCS S 0804-Y30R (светлый «рисовая бумага»), LRV 78 — 60 % база
- Little Greene No. 105 (Slaked Lime), LRV 82 — 60 % база
- Tikkurila V484 (Driftwood), LRV 47 — 30 % второй цвет — Т9, Т16, Т19
- Farrow & Ball No. 298 (Bancha), LRV 14 — 10 % акцент — Т18
- NCS S 7005-Y20R (тёмный орех), LRV 9 — 10 % акцент
- Tikkurila F485 (Damask), LRV 83 — 60 % база — Т2, Т8, Т14
- Tikkurila X447 (Sea Smoke), LRV 63 — 30 % второй цвет — Т1, Т4, Т7, Т11, Т12, Т13, Т17
- NCS S 2005-Y30R (песочный грейж), LRV 55 — 30 % второй цвет — Т3
- NCS S 5010-G70Y (приглушённая олива), LRV 22 — 10 % акцент — Т5, Т6
- NCS S 1002-Y50R (тёплый светлый грейж), LRV 74 — текстиль — Т10

Допущения и предложения на листе. Основа листа: размеры помещений и положение проёмов введены заказчиком в брифе, на объекте не замерены (К-1); высота потолка 2700 мм — по брифу заказчика, не замерена (К-2); толщины стен приняты по брифу: наружные 200 мм, внутренние 150 мм — не обмерены (К-1); тип дома монолитный, перекрытие 200 мм — по брифу заказчика, документов нет (К-3); планировка (стены, проёмы, объединение кухни и гостиной, расширение санузла) — по брифу без обмера и плана БТИ (К-7); разрешённая мощность 10 кВт принята, ТУ не переданы (К-8); вентканалы приняты, в брифе не заданы (К-9); подрайон климата не задан — принят не северный (жилые от 2,5 м) (К-10). См. лист открытых вопросов (лист 5, записи К-1–К-3, К-7–К-10).

Изм.	Кол.уч	Лист	№ док.	Подп.	Дата
Разраб.		Кырлан А.С.			21.10.26
Пров.					
ГИП					
Н. контр.					
Утв.					

ГД-2026-011-АИ

Квартира 56 м²

ЖК «Северный парк», Москва

Дизайн-проект интерьера

Стадия	Лист	Листов
РП	47	83

Концепция декора и визуализации

М б/м


Кырлан Александр Сергеевич

выпуск 19.10.2026 № 1c3e34763b · стр. 56 из 117

План текстиля и декора

Шторы и карнизы, ковры, картины и зеркала, растения · размеры в мм от чистовых стен и чистого пола · марки — по ведомостям

ПРЕДВАРИТЕЛЬНО · не для производства работ · открыто пунктов: 10 (реестр — л. 5)

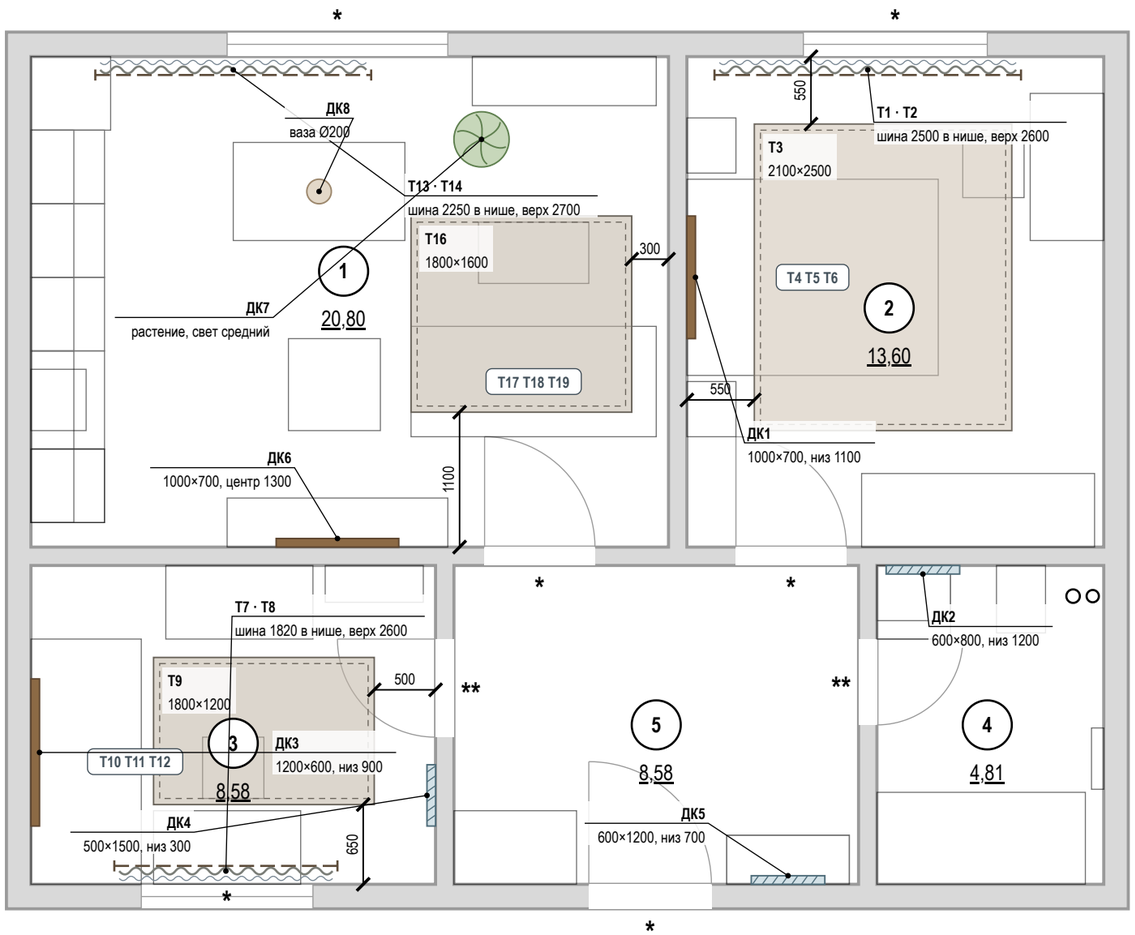

Условные обозначения

- ковёр — габарит в масштабе, цвет изделия
- шина или карниз штор (выше плоскости разреза)
- портьеры (штора-волна)
- тюль (на плане — волнистая линия)
- римская или рулонная штора в проёме
- картина на стене — ширина в масштабе
- зеркало на стене — ширина в масштабе
- растение в кашпо — диаметр в масштабе
- ваза, настольный декор
- подушки, пледы — марки на мебели
- привязка от чистовой стены, мм
- (1) номер помещения, площадь м²
- стены (подложка обмера)
- * «*» — принято, не замерено и не подтверждено
- ** «**» — предложение проектировщика, заказчиком не утверждено

Т1, ДК1 — марки по ведомостям текстиля и декора

Экспликация помещений

лист 13 · на плане — номера в марках

Окна: шина → полотно, мм

Поз.	Шина	Верх шины	Полотно, низ
Т13, Т14	2250	2700, ниша	2690, низ 10
Т1, Т2	2500	2600, ниша	2590, низ 10
Т7, Т8	1820	2600, ниша	2590, низ 10

Развеска: высоты от пола, мм

Поз.	Пом.	Ш×В	Центр	Низ	Стена
ДК1	2	1000×700	1450	1100	Г
ДК2	4	600×800	1600	1200	А
ДК3	3	1200×600	1200	900	Г
ДК4	3	500×1500	1050	300	Б
ДК5	5	600×1200	1300	700	В
ДК6	1	1000×700	1300	950	В

Допущения и предложения на листе. Основа листа: размеры помещений и положение проёмов введены заказчиком в брифе, на объекте не замерены (К-1); высота потолка 2700 мм — по брифу заказчика, не замерена (К-2); толщины стен приняты по брифу: наружные 200 мм, внутренние 150 мм — не обмерены (К-1); тип дома монолитный, перекрытие 200 мм — по брифу заказчика, документов нет (К-3); планировка (стены, проёмы, объединение кухни и гостиной, расширение санузла) — по брифу без обмера и плана БТИ (К-7); разрешённая мощность 10 кВт принята, ТУ не переданы (К-8); вентканалы приняты, в брифе не заданы (К-9); подрайон климата не задан — принят не северный (жилые от 2,5 м) (К-10). Знак «*» — принято, не замерено и не подтверждено (замерить на объекте): К-4: Ст К1-1 — положение стояка канализации — по брифу заказчика, не замерено; Ст В1-1 — положение стояка холодной воды — по брифу заказчика, не замерено. Знак «**» — предложение проектировщика, заказчиком не утверждено (согласовать с заказчиком). См. лист открытых вопросов (лист 5, записи К-1–К-5, К-7–К-10).

Примечания

1. Размеры — в мм. Отступы ковров — от чистовых стен; высоты картин и зеркал — от чистого пола до центра или низа рамы.
2. Шторы — на шинах в нишах потолка (ниша — план потолков, лист 36); закладная под шину — до обшивки ГКЛ. Схемы окон, длины полотен и сборка — лист 49.
3. Картины и зеркала массой более 5 кг — на анкеры по основанию, нагрузка крепежа не меньше двойной массы изделия; на ГКЛ — только по закладной. Декор не перекрывает розетки и выключатели.
4. Ковры на гладком полу — на противоскользящей подложке.
5. Мебель — по плану расстановки мебели (лист 17); ведомость текстиля — лист 50, ведомость декора и схемы развески — лист 51.
6. Знак «*» у проёма — допущение: положение проёма не замерено (окно пом. 1, стена А; дверь пом. 1, стена В; окно пом. 2, стена А; дверь пом. 2, стена В; окно пом. 3, стена В; дверь пом. 5, стена В); размер напечатан как принятый. Реестр: лист 5, вопрос К-1.
7. Номера помещений — по экспликации (лист 13); наименования и площади на этом листе не дублируются.
8. Марки текстиля «Т» и декора «Д» относятся только к листам текстиля и декора; индексы трубопроводов Т1–Т4 — на листах ВК и ОВ.

1000 мм · печать 1:1

Изм.	Кол.уч	Лист	№ док.	Подп.	Дата
Разраб.		Кырлан А.С.			21.10.26
Пров.					
ГИП					
Н. контр.					
Утв.					

ГД-2026-011-АИ

Квартира 56 м²

ЖК «Северный парк», Москва

Дизайн-проект интерьера

Стадия	Лист	Листов
РП	48	83

План текстиля и декора

М 1:50

Кырлан Александр Сергеевич

выпуск 19.10.2026 № 1c3e34763b · стр. 57 из 117

08

Декор и текстиль


Кырлан Александр Сергеевич

выпуск 19.10.2026 № 1c3e34763b · стр. 58 из 117


Шторы и карнизы

Схемы окон «шина → полотно» (М 1:50) · отметки от чистого пола помещения · размеры в мм


Окно 1* — Гостиная-кухня (пом. 1): Т13, Т14 (М 1:50)

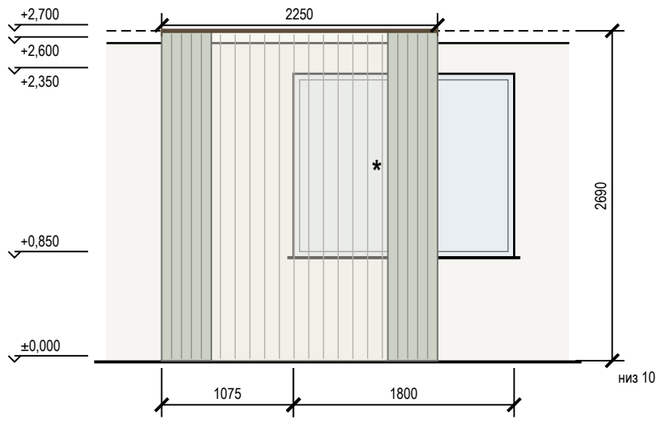

Окно 1* — Спальня (пом. 2): Т1, Т2 (М 1:50)

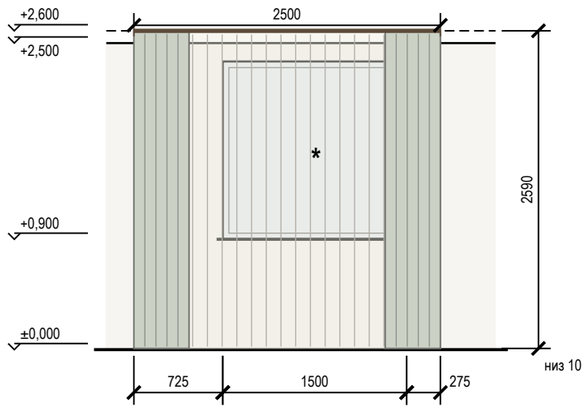

Окно 1* — Детская (пом. 3): Т7, Т8 (М 1:50)

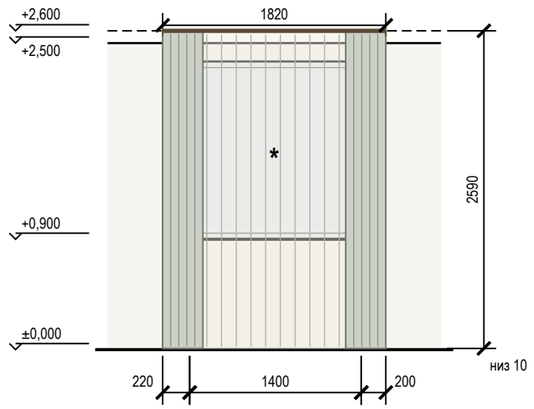

Карта окон: окно → шина → полотно

Поз.	Окно, пом.	Проём Ш×В, подоконник	Верх ниши	Изделие	Шина / карниз: длина, крепление	Верх шины	Полотно: длина, низ	Управление
Т13	1*, пом. 1	1800×1500, подок. 850	+2,700	портьеры	шина, 2250, в нише потолка, вынос 150	+2,700	2690, низ 10 (парит)	вручную
Т14	1*, пом. 1	1800×1500, подок. 850	+2,700	тюль	шина, 2250, в нише потолка, вынос 150	+2,700	2690, низ 10 (парит)	вручную
Т1	1*, пом. 2	1500×1450, подок. 900	+2,600	портьеры	шина, 2500, в нише потолка, вынос 150	+2,600	2590, низ 10 (парит)	вручную
Т2	1*, пом. 2	1500×1450, подок. 900	+2,600	тюль	шина, 2500, в нише потолка, вынос 150	+2,600	2590, низ 10 (парит)	вручную
Т7	1*, пом. 3	1400×1450, подок. 900	+2,600	портьеры	шина, 1820, в нише потолка, вынос 150	+2,600	2590, низ 10 (парит)	вручную
Т8	1*, пом. 3	1400×1450, подок. 900	+2,600	тюль	шина, 1820, в нише потолка, вынос 150	+2,600	2590, низ 10 (парит)	вручную

Задания смежникам

Кому	Задание	Пом.
Гипсокартонщик	окно 1 (1800×1500, Т13, Т14): ниша под шторы 150×100, верх +2,700; закладная под шину L 2250 по всей длине — до обшивки	1
Гипсокартонщик	окно 1 (1500×1450, Т1, Т2): ниша под шторы 150×100, верх +2,600; закладная под шину L 2500 по всей длине — до обшивки	2
Гипсокартонщик	окно 1 (1400×1450, Т7, Т8): ниша под шторы 150×100, верх +2,600; закладная под шину L 1820 по всей длине — до обшивки	3
Электрик	выводы под электрокарнизы не требуются (управление вручную)	

Условные обозначения

- портьеры в открытом положении
- римская штора: сложена / опущена
- верх ниши под шторы в потолке
- * — «*» — принято, не замерено и не подтверждено
- тюль (на виде окна — прозрачная плашка)
- шина или карниз на отметке верха
- оконный проём

Допущения и предложения на листе

Основа листа: размеры помещений и положение проёмов введены заказчиком в брифе, на объекте не замерены (К-1); высота потолка 2700 мм — по брифу заказчика, не замерена (К-2); толщины стен приняты по брифу: наружные 200 мм, внутренние 150 мм — не обмерены (К-1); тип дома монолитный, перекрытие 200 мм — по брифу заказчика, документов нет (К-3); планировка (стены, проёмы, объединение кухни и гостиной, расширение санузла) — по брифу без обмера и плана БТИ (К-7); разрешённая мощность 10 кВт принята, ТУ не переданы (К-8); вентканалы приняты, в брифе не заданы (К-9); подрайон климата не задан — принят не северный (жилые от 2,5 м) (К-10).

Знак «*» — принято, не замерено и не подтверждено (замерить на объекте): К-1: окно пом. 1 (стена А) — окно: положение, ширина, высота и подоконник — по брифу заказчика, не замерены; ограждение 900 мм — предложение исполнителя; дверь пом. 1 (стена В) — проём в существующей стене между пом. 1 и 5: положение и ширина — по брифу заказчика, не замерены; окно пом. 2 (стена А), 3 (В) — окно: положение, ширина, высота и подоконник — по брифу заказчика, не замерены; дверь пом. 2 (стена В) — проём в существующей стене между пом. 2 и 5: положение и ширина — по брифу заказчика, не замерены.

Знак «**» — предложение проектировщика, заказчиком не утверждено (согласовать с заказчиком): К-5: дверь пом. 3 (стена Б) — дверь в новой перегородке: проём по брифу, короб скрытой двери и размер в свету — после выбора модели и утверждения перегородки (К-5).

См. лист открытых вопросов (лист 5, записи К-1–К-3, К-5, К-7–К-10).

Примечания

1. Отметки — от чистого пола помещения; размеры — мм. Длины полотен уточняются замером после чистовой отделки пола и потолка, до раскроя.
2. Шины в нишах потолка: закладная (брус или профиль) по всей длине ниши — до обшивки ГКЛ; ниша и её отметка — узел ниши на плане потолков (лист 36).
3. Шина в нише — на отметке верха ниши (крепление к закладной в потолке ниши); длина полотна — от верха шины до чистого пола за вычетом зазора.
4. Полотно портьер «парит» над полом на 10 мм; сборка портьер — 2,0, тюля — 2,5 (ширина полотна — в ведомости текстиля).
5. Электрокарнизы не предусмотрены; при замене на электропривод — вывод кабеля в нише у края шины (задание электрику).
6. Знак «*» у проёма — допущение: положение проёма не замерено (окно пом. 1, стена А; окно пом. 2, стена А; окно пом. 3, стена В); размер напечатан как принятый. Реестр: лист 5, вопрос К-1.
7. Длины шин и полотен окон 1 (пом. 1), 1 (пом. 2), 1 (пом. 3) выведены из размеров и положения проёма, а они — допущение: до раскроя полотен проём замерить, длины сверить.
8. Марки изделий — по плану текстиля и декора (лист 48) и ведомости текстиля (лист 50).

Изм.	Кол.уч	Лист	№ док.	Подп.	Дата
Разраб.		Кырлан А.С.			21.10.26
Пров.					
ГИП					
Н. контр.					
Утв.					

ГД-2026-011-АИ

Квартира 56 м²

ЖК «Северный парк», Москва

Дизайн-проект интерьера

Стадия	Лист	Листов
РП	49	83

Шторы и карнизы

М б/м

Кырлан Александр Сергеевич

выпуск 19.10.2026 № 1c3e34763b · стр. 59 из 117

ПРЕДВАРИТЕЛЬНО · не для производства работ · открыто пунктов: 10 (реестр — л. 5)

Ведомость текстиля

Шторы, тюль, римские шторы, ковры, подушки и пледы · размеры в мм · марки — по плану текстиля и декора

Текстиль: шторы, ковры, подушки, пледы


Поз.	Пом.	Изделие	Размер, мм	Ткань, состав, плотность	Сборка, ширина полотна		Цвет (система, код)	Кол.	Примечание
T1	2	Портьеры-волна	шина 2500 × полотно 2590	лён с блэкаут-подкладкой; лён 100 %; 320 г/м²	× 2, ширина 5000		Tikkurila X447 (Sea Smoke)	2	низ 10 (парит); в нише потолка
T2	2	Тюль	шина 2500 × полотно 2590	вуаль; полиэстер 100 %	× 2,5, ширина 6250		Tikkurila F485 (Damask)	1	низ 10 (парит); в нише потолка
T3	2	Ковёр под кроватью, шерсть	2100×2500	шерсть, ручное ткачество; шерсть 80 %, хлопок 20 %			NCS S 2005-Y30R (песочный грейж)	1	противоскользящая подложка; ворс 10 мм
T4	2	Подушки декоративные на кровать	500×500	лён 100 %			Tikkurila X447 (Sea Smoke)	3	на Сп1
T5	2	Подушки на кровать, акцент	400×600	хлопковый бархат 100 %			NCS S 5010-G70Y (приглушённая олива)	2	на Сп1
T6	2	Плед на кровать	1300×1700	шерсть меринос 100 %			NCS S 5010-G70Y (приглушённая олива)	1	на Сп1
T7	3	Портьеры-волна	шина 1820 × полотно 2590	лён с блэкаут-подкладкой; лён 100 %; 320 г/м²	× 2, ширина 3640		Tikkurila X447 (Sea Smoke)	2	низ 10 (парит); в нише потолка
T8	3	Тюль	шина 1820 × полотно 2590	вуаль; полиэстер 100 %	× 2,5, ширина 4550		Tikkurila F485 (Damask)	1	низ 10 (парит); в нише потолка
T9	3	Ковёр игровой, шерсть	1800×1200	шерсть, плоское плетение; шерсть 100 %			Tikkurila V484 (Driftwood)	1	противоскользящая подложка; ворс 8 мм
T10	3	Подушки декоративные на кровать	500×500	букле (шерсть 60 %, полиэстер 40 %)			NCS S 1002-Y50R (тёплый светлый грейж)	3	на Дт1
T11	3	Подушки на кровать, акцент	400×600	хлопковый бархат 100 %			Tikkurila X447 (Sea Smoke)	2	на Дт1
T12	3	Плед на кровать	1300×1700	шерсть меринос 100 %			Tikkurila X447 (Sea Smoke)	1	на Дт1
T13	1	Портьеры-волна (гостиная)	шина 2250 × полотно 2690	лён 70 %, вискоза 30 %; 280 г/м²	× 2, ширина 4500		Tikkurila X447 (Sea Smoke)	2	низ 10 (парит); в нише потолка
T14	1	Тюль (гостиная)	шина 2250 × полотно 2690	вуаль; полиэстер 100 %	× 2,5, ширина 5625		Tikkurila F485 (Damask)	1	низ 10 (парит); в нише потолка
T16	1	Ковёр в зоне отдыха, джут с шерстью	1800×1600	шерсть, петля; шерсть 100 %			Tikkurila V484 (Driftwood)	1	противоскользящая подложка; ворс низкий
T17	1	Подушки на диван	500×500	букле (шерсть 60 %, полиэстер 40 %)			Tikkurila X447 (Sea Smoke)	3	на Гс2
T18	1	Подушки на диван, акцент	400×600	хлопковый бархат 100 %			Farrow & Ball No. 298 (Bancha)	2	на Гс2
T19	1	Плед на диван	1300×1700	альпака 50 %, шерсть 50 %			Tikkurila V484 (Driftwood)	1	на Гс2

образец цвета — по HEX производителя краски, справочно

Итого: шторы и тюль — 9 шт.; ковры и дорожки — 3 шт.; подушки, пледы, покрывала — 18 шт.


Образцы по помещениям

1. Гостиная-кухня

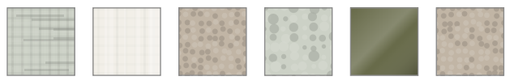


T13 T14 T16 T17 T18 T19

2. Спальня

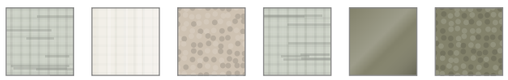

T1 T2 T3 T4 T5 T6

3. Детская

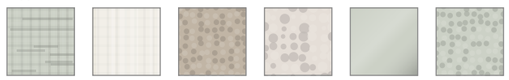

T7 T8 T9 T10 T11 T12

Примечания

1. Коды цвета — ориентир подбора по веерам производителей красок; ткань утверждается по образцу при дневном свете и при свете проекта 2700–3000 K.
2. Размеры полотен — по замеру после чистовой отделки пола и потолка; ширина полотна указана с учётом сборки, без припусков на швы. Схемы окон и отметки шин лист 49.
3. Портьеры и тюль — на тесьме «волна» по системе шины; блэкаут — подкладкой. Ковры — на противоскользящей подложке.
4. Замена изделия — аналогом по характеристикам (состав, плотность, размер, цвет по образцу) с согласованием автора проекта.
5. Места изделий — план текстиля и декора (лист 48); подушки и пледы — по марке мебели.

Допущения и предложения на листе

Основа листа: размеры помещений и положение проёмов введены заказчиком в брифе, на объекте не замерены (К-1); высота потолка 2700 мм — по брифу заказчика, не замерена (К-2); толщины стен приняты по брифу: наружные 200 мм, внутренние 150 мм — не обмерены (К-1); тип дома монолитный, перекрытие 200 мм — по брифу заказчика, документов нет (К-3); планировка (стены, проёмы, объединение кухни и гостиной, расширение санузла) — по брифу без обмера и плана БТИ (К-7); разрешённая мощность 10 кВт принята, ТУ не переданы (К-8); вентканалы приняты, в брифе не заданы (К-9); подрайон климата не задан — принят не северный (жилые от 2,5 м) (К-10).
См. лист открытых вопросов (лист 5, записи К-1–К-3, К-7–К-10).

Изм.	Кол.уч	Лист	№ док.	Подп.	Дата
Разраб.		Кырлан А.С.			21.10.26
Пров.					
ГИП					
Н. контр.					
Утв.					

ГД-2026-011-АИ

Квартира 56 м²

ЖК «Северный парк», Москва

Дизайн-проект интерьера

Стадия	Лист	Листов
РП	50	83

Ведомость текстиля

М б/м

Кырлан Александр Сергеевич

Ведомость декора. Схемы развески

Картины, зеркала, растения, настольный декор · схемы развески (М 1:100) · высоты — мм от чистого пола


ПРЕДВАРИТЕЛЬНО · не для производства работ · открыто пунктов: 10 (реестр — л. 5)

Декор: картины, зеркала, растения, предметы


картина · зеркало · мебель под изделием

Поз.	Пом.	Предмет	Размер, мм	Место: стена, высота от пола, мм	Масса, кг	Крепёж и основание	Свет места, отделка	Кол.
ДК1	2	Картина над кроватью: Ветка цветущей сакуры, акварель на тёплой бумаге	1000×700	стена Г, привязка 1300; низ 1100, центр 1450; над Сп1	4	подвес по основанию, 2 точки	рама — дуб	1
ДК2	4	Зеркало над умывальником, влагостойкое, с подсветкой	600×800	стена А, привязка 75; низ 1200, центр 1600; над Сн3		подвес по основанию, 2 точки		1
ДК3	3	Картина над кроватью: Серый кот спит на подоконнике у окна с бумажной ширмой, детская иллюстрация, гуашь	1200×600	стена Г, привязка 925; низ 900, центр 1200; над Дт1	4	подвес по основанию, 2 точки	рама — дуб	1
ДК4	3	Зеркало в рост в тонкой чёрной раме	500×1500	стена Б, привязка 1625; низ 300, центр 1050	12	анкер для пустотелых оснований, 4 шт.; основание: перегородка — определить обмером до монтажа; нагрузка 30 кг	рама — чёрный матовый металл	1
ДК5	5	Зеркало над скамьёй, тонкая чёрная рама	600×1200	стена В, привязка 2425; низ 700, центр 1300	18	анкер, 4 шт.; основание: перегородка — определить обмером до монтажа; нагрузка 40 кг	рама — чёрный матовый металл	1
ДК6	1	Картина над консолью: Горный ручей среди камней в тумане, тушь суми-э на бумаге васи	1000×700	стена В, привязка 2000; центр 1300; над Гс5	6	анкер, 2 шт.; основание: перегородка — определить обмером до монтажа; нагрузка 15 кг		1
ДК7	1	Фикус каучуконосный в кашпо Ø450, глина	450×450	напольное			свет средний	1
ДК8	1	Ваза керамическая с одной веткой на обеденном столе	200×350	на Кх11 (обеденный стол)				1


ДК1 — Спальня (пом. 2), стена Г (М 1:100)

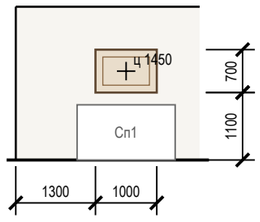


ДК2 — Санузел (пом. 4), стена А (М 1:100)

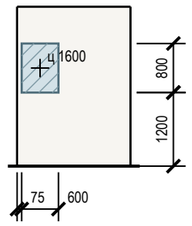


ДК3 — Детская (пом. 3), стена Г (М 1:100)

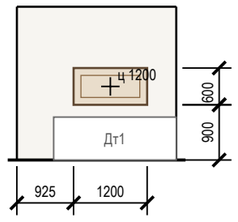


ДК4 — Детская (пом. 3), стена Б (М 1:100)

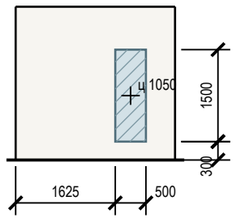

ДК5 — Прихожая (пом. 5), стена В (М 1:100)

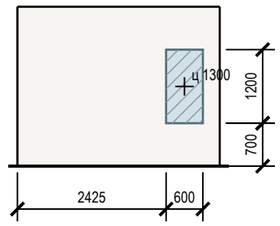

ДК6 — Гостиная-кухня (пом. 1), стена В (М 1:100)

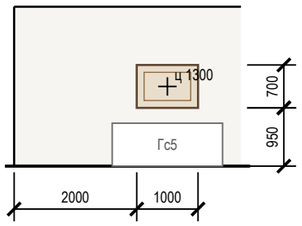

Допущения и предложения на листе

Основа листа: размеры помещений и положение проёмов введены заказчиком в брифе, на объекте не замерены (К-1); высота потолка 2700 мм — по брифу заказчика, не замерена (К-2); толщины стен приняты по брифу: наружные 200 мм, внутренние 150 мм — не обмерены (К-1); тип дома монолитный, перекрытие 200 мм — по брифу заказчика, документов нет (К-3); планировка (стены, проёмы, объединение кухни и гостиной, расширение санузла) — по брифу без обмера и плана БТИ (К-7); разрешённая мощность 10 кВт принята, ТУ не переданы (К-8); вентканалы приняты, в брифе не заданы (К-9); подрайон климата не задан — принят не северный (жилые от 2,5 м) (К-10).

См. лист открытых вопросов (лист 5, записи К-1–К-3, К-7–К-10).

Примечания

1. Высоты — от чистого пола помещения до низа изделия, «ц» — до центра; привязки — от чистовой грани угла стены, мм.
2. Над мебелью низ изделия — на 150–250 мм выше спинки или изголовья; без мебели центр — на 1450–1600 мм от пола.
3. Изделия до 5 кг — на два подвеса по основанию; тяжелее — на анкеры с нагрузкой не меньше двойной массы; на ГКЛ — только по закладной или анкеру для пустотелых оснований.
4. Зеркала в рост — с креплением от опрокидывания; в санузлах — влагостойкие, на клей для зеркал и нейтральный силикон.
5. Места изделий — план текстиля и декора (лист 48).

Изм.	Кол.уч	Лист	№ док.	Подп.	Дата
Разраб.		Кырлан А.С.			21.10.26
Пров.					
ГИП					
Н. контр.					
Утв.					

ГД-2026-011-АИ

Квартира 56 м²

ЖК «Северный парк», Москва

Дизайн-проект интерьера

Стадия	Лист	Листов
РП	51	83

Ведомость декора. Схемы развески

М б/м


Кырлан Александр Сергеевич

выпуск 19.10.2026 № 1c3e34763b · стр. 61 из 117

Встроенная мебель. Схема расположения

встроенная и корпусная мебель на заказ, кухонный гарнитур · размеры в мм · марки — по ведомости изделий

ПРЕДВАРИТЕЛЬНО · не для производства работ · открыто пунктов: 10 (реестр — л. 5)

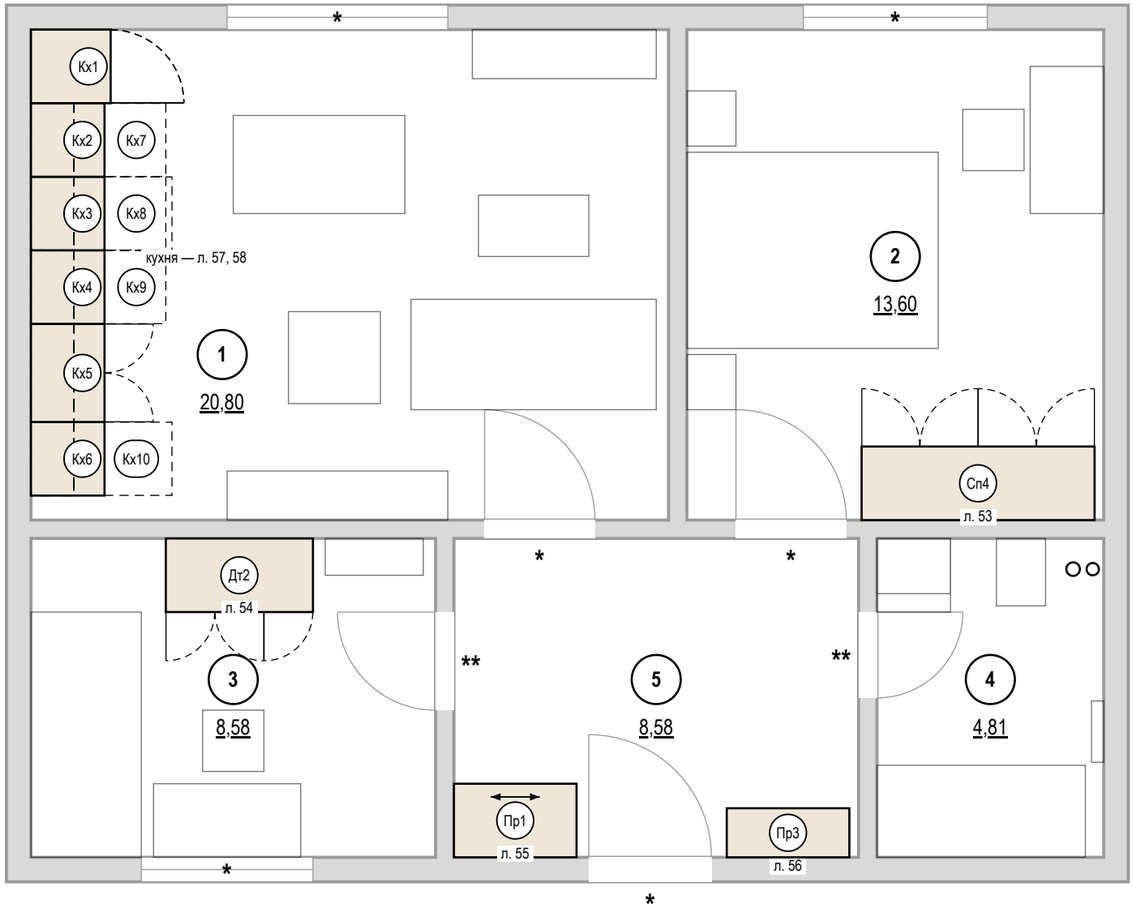

Ведомость изделий

Марка	Наименование	Пом.	Ш×Г×В, мм	Лист
Сп4	Шкаф распашной	2	1900×600×2400	53
Дт2	Шкаф распашной	3	1200×600×2200	54
Пр1	Шкаф-купе	5	1000×600×2510	55
Пр3	Система хранения	5	1000×400×500	56
Кх6	Модуль нижний: ПММ	1	600×600×900	57
Кх10	Модуль навесной: полки, сушка	1	1400×350×900	57
Кх5	Модуль нижний: мойка	1	800×600×900	57
Кх4	Модуль нижний: ящики	1	600×600×900	57
Кх9	Модуль навесной: полки	1	600×350×900	57
Кх3	Модуль нижний: духовой шкаф, варочная	1	600×600×900	57
Кх8	Модуль навесной: полки	1	600×350×800	57
Кх2	Модуль нижний: ящики	1	600×600×900	57
Кх7	Модуль навесной: полки	1	600×350×900	57
Кх1	Пенал: холодильник встр.	1	600×650×2350	57

Условные обозначения

- изделие мебельщика: корпус на полу
- навесной модуль (невидимый контур)
- открывание распашного фасада
- зона выдвижения ящика, двери техники
- дверь купе, стрелка — направление движения
- П5 — марка изделия, под ней — лист изделия
- * — «*» — принято, не замерено и не подтверждено
- ** — «**» — предложение проектировщика, заказчиком не утверждено

Допущения и предложения на листе. Основа листа: размеры помещений и положение проёмов введены заказчиком в брифе, на объекте не замерены (К-1); высота потолка 2700 мм — по брифу заказчика, не замерена (К-2); толщины стен приняты по брифу: наружные 200 мм, внутренние 150 мм — не обмерены (К-1); тип дома монолитный, перекрытие 200 мм — по брифу заказчика, документов нет (К-3); планировка (стены, проёмы, объединение кухни и гостиной, расширение санузла) — по брифу без обмера и плана БТИ (К-7); разрешённая мощность 10 кВт принята, ТУ не переданы (К-8); вентканалы приняты, в брифе не заданы (К-9); подрайон климата не задан — принят не северный (жилые от 2,5 м) (К-10). Знак «*» — принято, не замерено и не подтверждено (замерить на объекте): К-4: Ст К1-1 — положение стояка канализации — по брифу заказчика, не замерено; Ст В1-1 — положение стояка холодной воды — по брифу заказчика, не замерено. Знак «**» — предложение проектировщика, заказчиком не утверждено (согласовать с заказчиком). См. лист открытых вопросов (лист 5, записи К-1–К-5, К-7–К-10).

Примечания

1. Изделия — по чистовым размерам помещений; перед раскроем — контрольный замер цеха после чистовой отделки стен, пола и потолка.
2. Открывание фасадов и выдвижение ящиков показано в открытом положении: зоны не пересекают двери, радиаторы, выключатели и проходы.
3. Стояки и счётчики за мебелью — с сервисным люком; газовые трубы мебелью не зашиваются.
4. Покупная мебель — по плану расстановки мебели и спецификации дизайнера; здесь — подложкой.
5. Знак «*» у проёма — положение не замерено; реестр: лист 5, вопрос К-1.

1000 мм · печать 1:1

Изм.	Кол.уч	Лист	№ док.	Подп.	Дата
Разраб.		Кырлан А.С.			21.10.26
Пров.					
ГИП					
Н. контр.					
Утв.					

ГД-2026-011-АИ

Квартира 56 м²

ЖК «Северный парк», Москва

Дизайн-проект интерьера

Стадия	Лист	Листов
РП	52	83

Встроенная мебель. Схема расположения

М 1:50

Кырлан Александр Сергеевич


выпуск 19.10.2026 № 1c3e34763b · стр. 62 из 117

Шкаф распашной Сп4


Спальня (пом. 2) · вид из помещения · размеры в мм, отметки в м

ПРЕДВАРИТЕЛЬНО · не для производства работ · открыто пунктов: 10 (реестр — л. 5)


Вид с фасадами

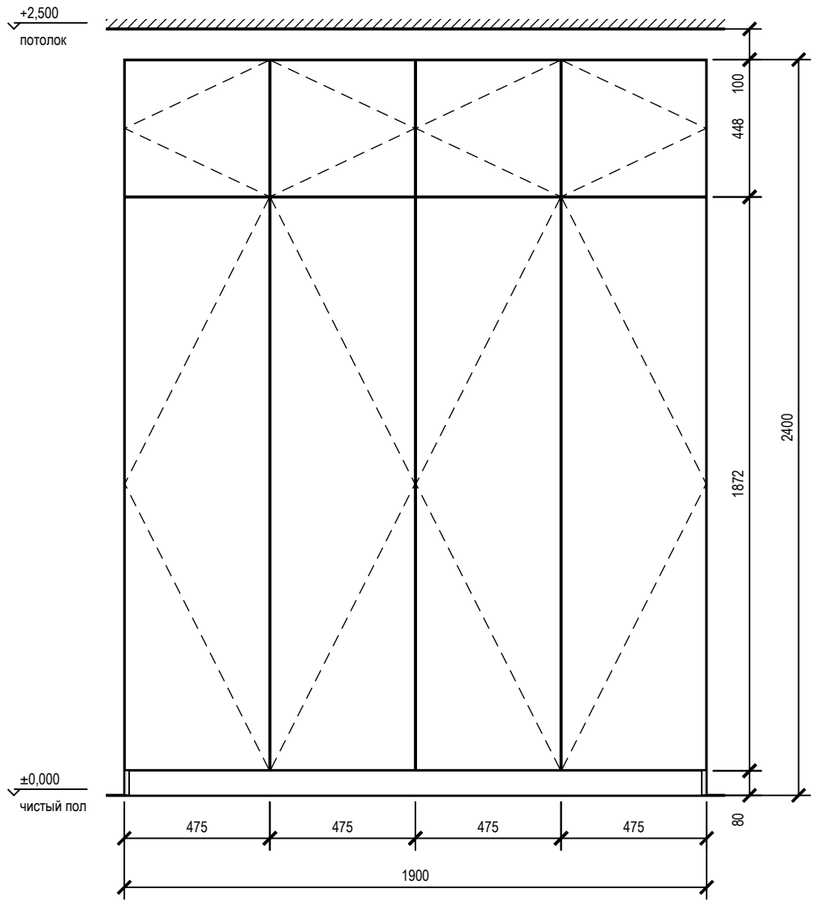


Вид без фасадов

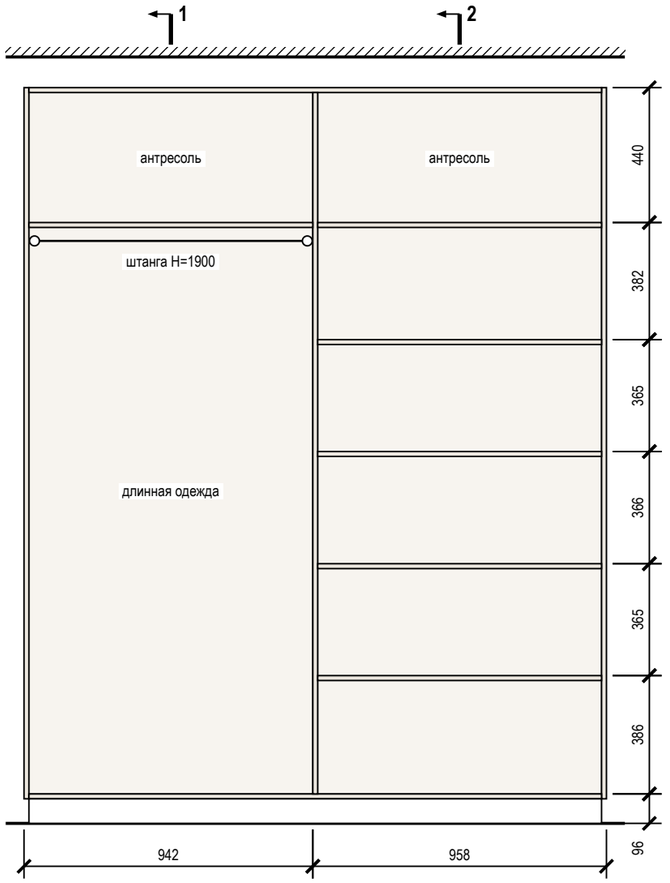

Разрез 1-1

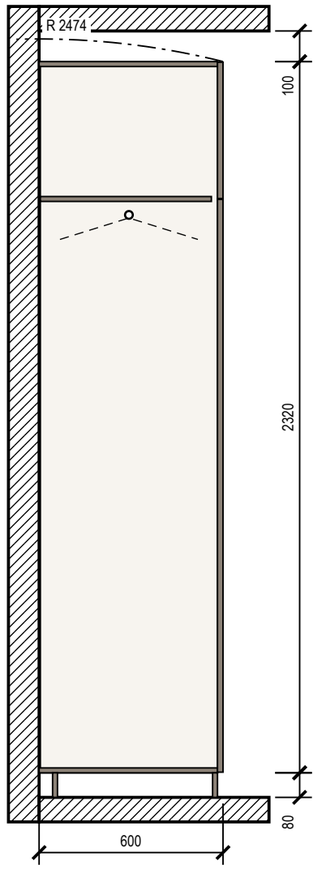

Разрез 2-2

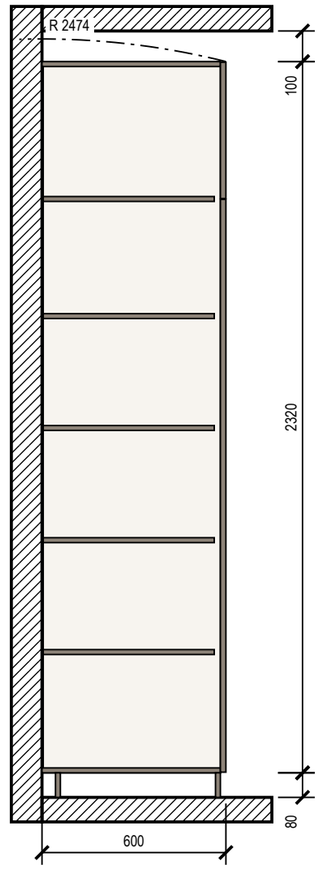

Примечания

1. Размеры — в мм по чистовой отделке; изделие 1900×600×2400 (Ш×Г×В). Перед раскроем — контрольный замер цеха после чистовой отделки стен, пола и потолка.
2. Корпус — ЛДСП 16 мм, задняя стенка ХДФ 4 мм в паз, цоколь 80 мм на регулируемых опорах; фасады — МДФ, эмаль матовая 18 мм накладные, цвет — по колерной карте; петли с доводчиком: фасад 1869 мм — 4 петли, фасад 445 мм — 2 петли.
3. Кромка: скрытые торцы 0,4 мм, видимые 2 мм (ПВХ/АБС).
4. Номинальные зазоры: между фасадами 3 мм, фасад — стена и фасад — потолок не менее 3 мм, фасад ящика — стойка 2 мм.
5. Ящики — направляющие полного выдвижения NL 550 (внутренняя глубина 578 мм ≥ NL + 3); присадка по 32-й системе — выполняет цех.
6. Зазор до потолка 100 мм — закрыть планкой в цвет корпуса при монтаже.
7. Подъём корпуса: диагональ боковины $\sqrt{(2400^2 + 600^2)} = 2474$ мм < 2500 мм до потолка — корпус собирается лёжа и поднимается поворотом.
8. Крепление к стене от опрокидывания: уголок к стене, 2 шт.; основание стены и шаг анкеров — монтажная схема шкафов.

Условные обозначения

- фасад распашной: линии сходятся к стороне петель
- корпус и полки ЛДСП (вид на стену)
- задняя стенка ХДФ
- деталь в разрезе
- штанга для плечиков (на разрезе — плечики 450 мм)
- траектория угла корпуса при подъёме в проектное положение

Допущения и предложения на листе

Основа листа: размеры помещений и положение проёмов введены заказчиком в брифе, на объекте не замерены (К-1); высота потолка 2700 мм — по брифу заказчика, не замерена (К-2); толщины стен приняты по брифу: наружные 200 мм, внутренние 150 мм — не обмерены (К-1); тип дома монолитный, перекрытие 200 мм — по брифу заказчика, документов нет (К-3); планировка (стены, проёмы, объединение кухни и гостиной, расширение санузла) — по брифу без обмера и плана БТИ (К-7); разрешённая мощность 10 кВт принята, ТУ не переданы (К-8); вентканалы приняты, в брифе не заданы (К-9); подрайон климата не задан — принят не северный (жилые от 2,5 м) (К-10).
См. лист открытых вопросов (лист 5, записи К-1–К-3, К-7–К-10).

1000 мм · печать 1:1

Изм.	Кол.уч	Лист	№ док.	Подп.	Дата
Разраб.		Кырлан А.С.			21.10.26
Пров.					
ГИП					
Н. контр.					
Утв.					

ГД-2026-011-АИ

Квартира 56 м²

ЖК «Северный парк», Москва

Дизайн-проект интерьера

Стадия	Лист	Листов
РП	53	83

Шкаф распашной Сп4

М 1:20

Кырлан Александр Сергеевич


выпуск 19.10.2026 № 1c3e34763b · стр. 63 из 117

Шкаф распашной Дт2


Детская (пом. 3) · вид из помещения · размеры в мм, отметки в м

ПРЕДВАРИТЕЛЬНО · не для производства работ · открыто пунктов: 10 (реестр — л. 5)


Вид с фасадами

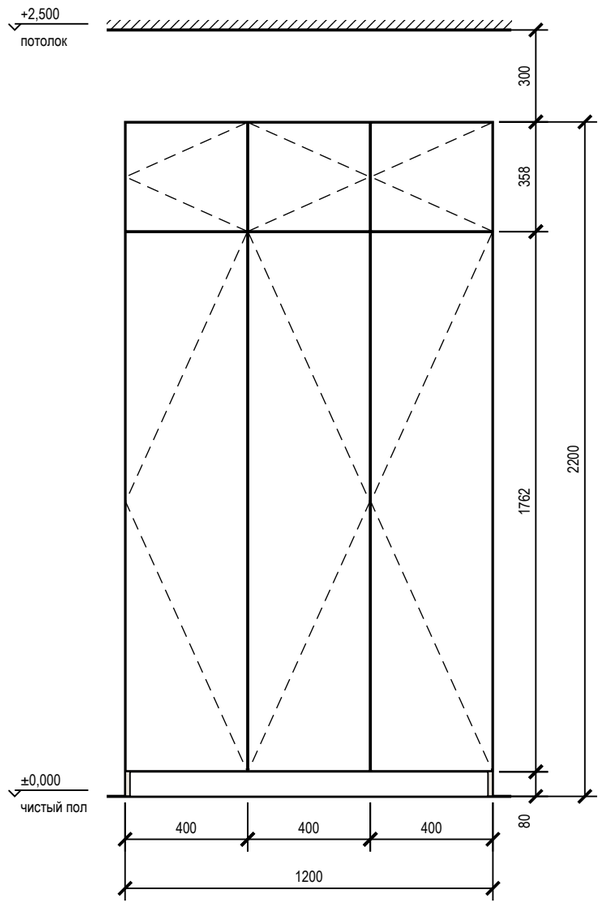


Вид без фасадов

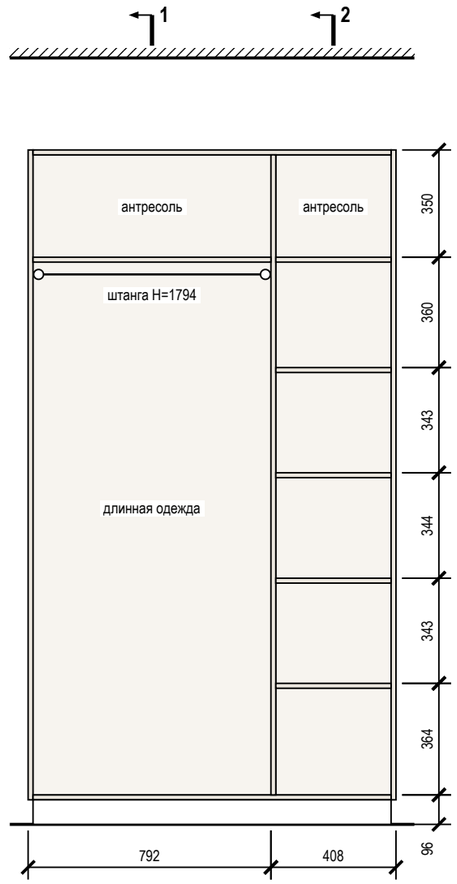

Разрез 1-1

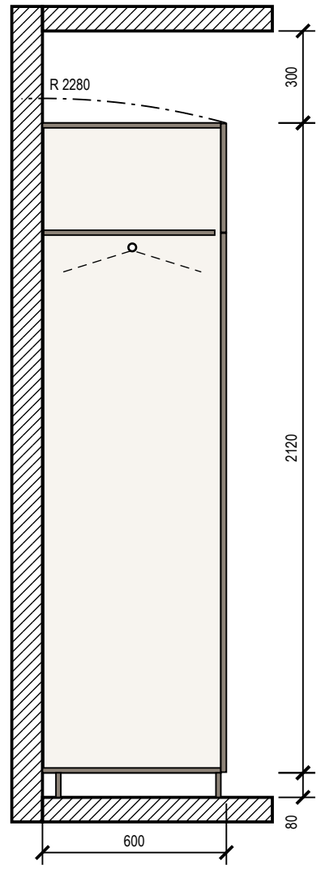

Разрез 2-2

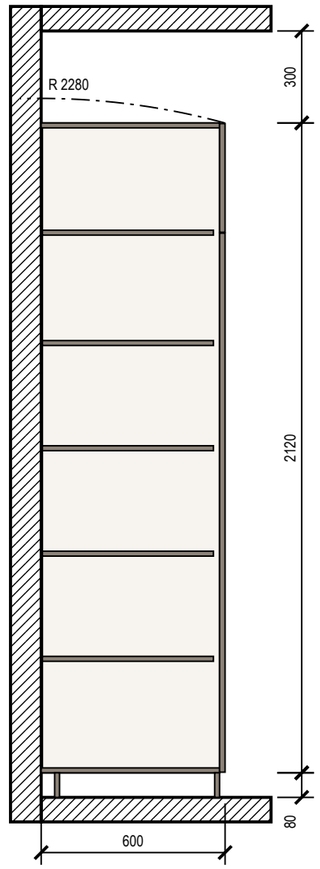

Примечания

1. Размеры — в мм по чистовой отделке; изделие 1200×600×2200 (Ш×Г×В). Перед раскроем — контрольный замер цеха после чистовой отделки стен, пола и потолка.
2. Корпус — ЛДСП 16 мм, задняя стенка ХДФ 4 мм в паз, цоколь 80 мм на регулируемых опорах; фасады — МДФ, эмаль матовая 18 мм накладные, цвет — по колерной карте; петли с доводчиком: фасад 1759 мм — 4 петли, фасад 355 мм — 2 петли.
3. Кромка: скрытые торцы 0,4 мм, видимые 2 мм (ПВХ/АБС).
4. Номинальные зазоры: между фасадами 3 мм, фасад — стена и фасад — потолок не менее 3 мм, фасад ящика — стойка 2 мм.
5. Ящики — направляющие полного выдвижения NL 550 (внутренняя глубина 578 мм ≥ NL + 3); присадка по 32-й системе — выполняет цех.
6. Зазор до потолка 300 мм.
7. Подъём корпуса: диагональ боковины $\sqrt{(2200^2 + 600^2)} = 2280$ мм < 2500 мм до потолка — корпус собирается лёжа и поднимается поворотом.
8. Крепление к стене от опрокидывания: уголок к стене, 2 шт.; основание стены и шаг анкеров — монтажная схема шкафов.

Условные обозначения

- фасад распашной: линии сходятся к стороне петель
- корпус и полки ЛДСП (вид на стену)
- задняя стенка ХДФ
- деталь в разрезе
- штанга для плечиков (на разрезе — плечики 450 мм)
- траектория угла корпуса при подъёме в проектное положение

Допущения и предложения на листе

Основа листа: размеры помещений и положение проёмов введены заказчиком в брифе, на объекте не замерены (К-1); высота потолка 2700 мм — по брифу заказчика, не замерена (К-2); толщины стен приняты по брифу: наружные 200 мм, внутренние 150 мм — не обмерены (К-1); тип дома монолитный, перекрытие 200 мм — по брифу заказчика, документов нет (К-3); планировка (стены, проёмы, объединение кухни и гостиной, расширение санузла) — по брифу без обмера и плана БТИ (К-7); разрешённая мощность 10 кВт принята, ТУ не переданы (К-8); вентканалы приняты, в брифе не заданы (К-9); подрайон климата не задан — принят не северный (жилые от 2,5 м) (К-10).
См. лист открытых вопросов (лист 5, записи К-1–К-3, К-7–К-10).

1000 мм · печать 1:1

Изм.	Кол.уч	Лист	№ док.	Подп.	Дата
Разраб.		Кырлан А.С.			21.10.26
Пров.					
ГИП					
Н. контр.					
Утв.					

ГД-2026-011-АИ

Квартира 56 м²

ЖК «Северный парк», Москва

Дизайн-проект интерьера

Стадия	Лист	Листов
РП	54	83

Шкаф распашной Дт2

М 1:20

Кырлан Александр Сергеевич


выпуск 19.10.2026 № 1c3e34763b · стр. 64 из 117

Шкаф-купе Пр1


Прихожая (пом. 5) · вид из помещения · размеры в мм, отметки в м

ПРЕДВАРИТЕЛЬНО · не для производства работ · открыто пунктов: 10 (реестр — л. 5)


Вид с фасадами

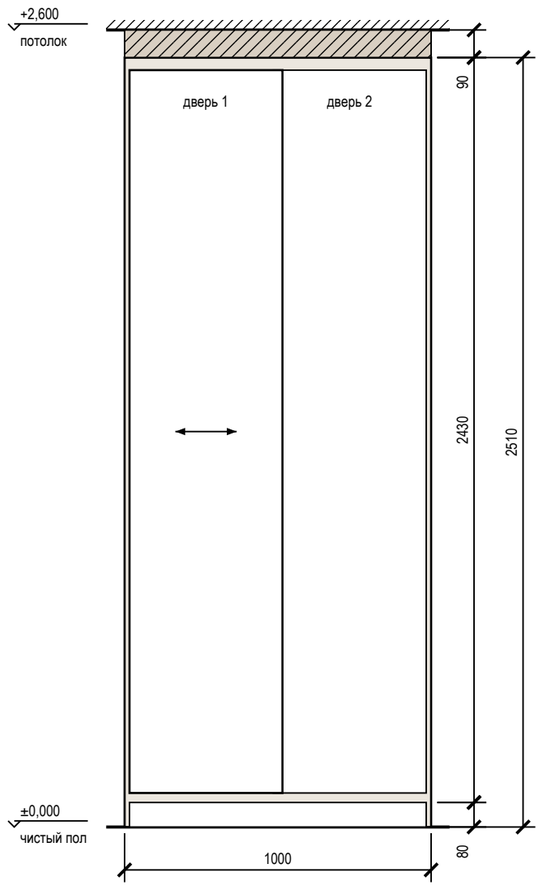


Вид без фасадов

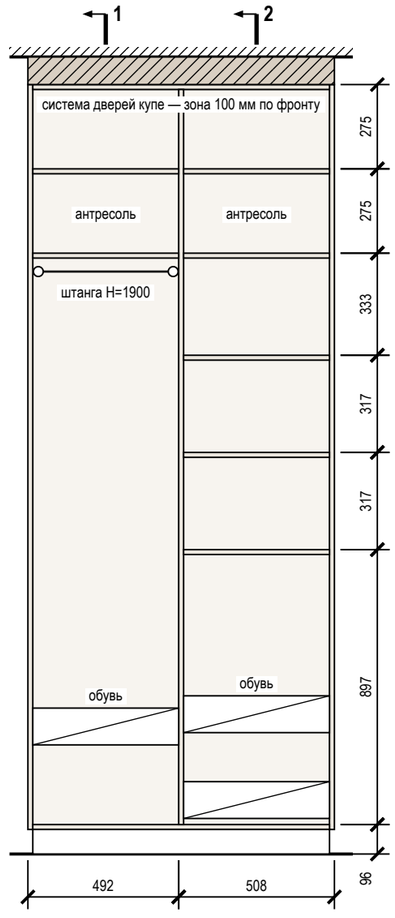

Разрез 1-1

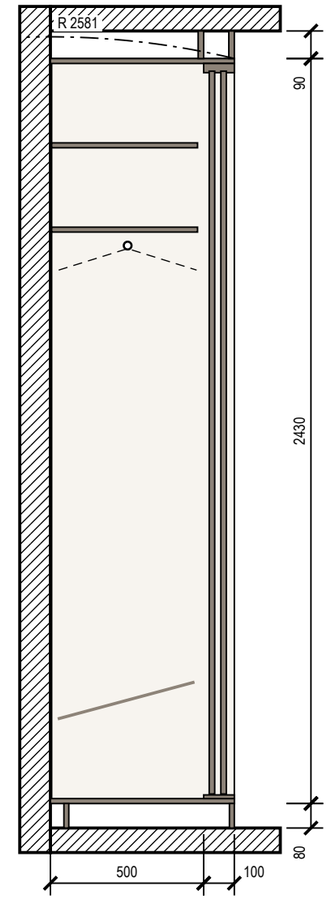

Разрез 2-2

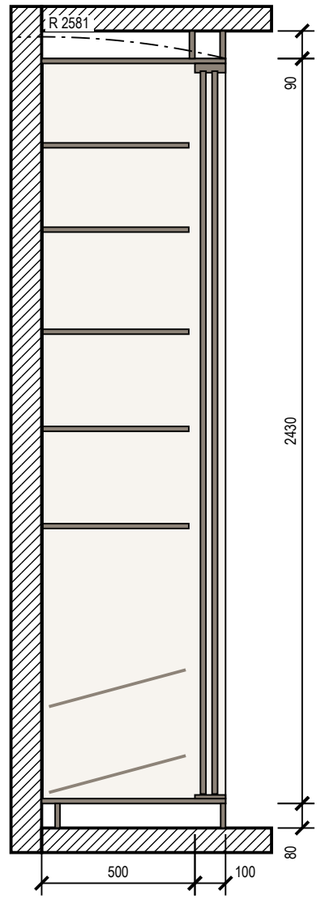

Примечания

1. Размеры — в мм по чистовой отделке; изделие 1000×600×2510 (Ш×Г×В). Перед раскроем — контрольный замер цеха после чистовой отделки стен, пола и потолка.
2. Корпус — ЛДСП 16 мм, задняя стенка ХДФ 4 мм в паз, цоколь 80 мм на регулируемых опорах; двери купе — ЛДСП 10 мм в алюминиевом профиле, нахлёст 30 мм, ширина двери 499 мм, высота — проём минус 40 мм; цвет — по колерной карте.
3. Кромка: скрытые торцы 0,4 мм, видимые 2 мм (ПВХ/АБС).
4. Номинальные зазоры: дверь купе — боковина 3 мм, фасад ящика — стойка 2 мм; ящики внутри купе — с накладкой 30 мм на стойке со стороны нахлёста дверей.
5. Ящики — направляющие полного выдвижения NL 450 (внутренняя глубина 496 мм ≥ NL + 3); присадка по 32-й системе — выполняет цех.
6. Компенсатор 90 мм — короб из ЛДСП по фронту и торцам, подгоняется к потолку при монтаже (припуск 20 мм), крепится к корпусу и к потолку.
7. Подъём корпуса: диагональ боковины $\sqrt{(2510^2 + 600^2)} = 2581$ мм < 2600 мм до потолка — корпус собирается лёжа и поднимается поворотом.
8. Крепление к стене от опрокидывания — уголки 2 шт. к несущему основанию (монтажная схема шкафов).

Условные обозначения

- дверь купе, стрелка — направление движения
- корпус и полки ЛДСП (вид на стену)
- задняя стенка ХДФ
- деталь в разрезе
- компенсатор — короб до потолка
- штанга для плечиков (на разрезе — плечики 450 мм)
- траектория угла корпуса при подъёме в проектное положение

Допущения и предложения на листе

Основа листа: размеры помещений и положение проёмов введены заказчиком в брифе, на объекте не замерены (К-1); высота потолка 2700 мм — по брифу заказчика, не замерена (К-2); толщины стен приняты по брифу: наружные 200 мм, внутренние 150 мм — не обмерены (К-1); тип дома монолитный, перекрытие 200 мм — по брифу заказчика, документов нет (К-3); планировка (стены, проёмы, объединение кухни и гостиной, расширение санузла) — по брифу без обмера и плана БТИ (К-7); разрешённая мощность 10 кВт принята, ТУ не переданы (К-8); вентканалы приняты, в брифе не заданы (К-9); подрайон климата не задан — принят не северный (жилые от 2,5 м) (К-10).
См. лист открытых вопросов (лист 5, записи К-1–К-3, К-7–К-10).

1000 мм · печать 1:1

Изм.	Кол.уч	Лист	№ док.	Подп.	Дата
Разраб.		Кырлан А.С.			21.10.26
Пров.					
ГИП					
Н. контр.					
Утв.					

ГД-2026-011-АИ

Квартира 56 м²

ЖК «Северный парк», Москва

Дизайн-проект интерьера

Стадия	Лист	Листов
РП	55	83

Шкаф-купе Пр1

М 1:20

Кырлан Александр Сергеевич


выпуск 19.10.2026 № 1c3e34763b · стр. 65 из 117

Система хранения Пр3


Прихожая (пом. 5) · вид из помещения · размеры в мм, отметки в м

ПРЕДВАРИТЕЛЬНО · не для производства работ · открыто пунктов: 10 (реестр — л. 5)


Общий вид

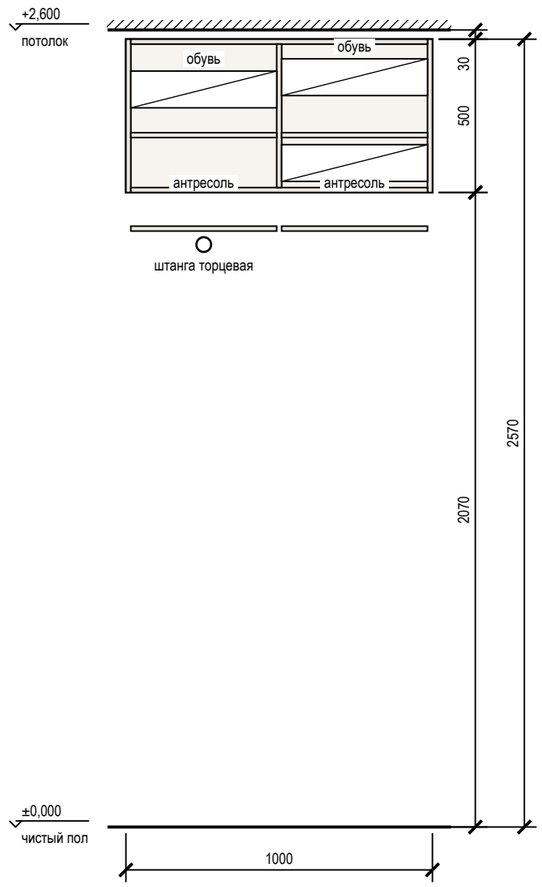


Наполнение, размеры в свету

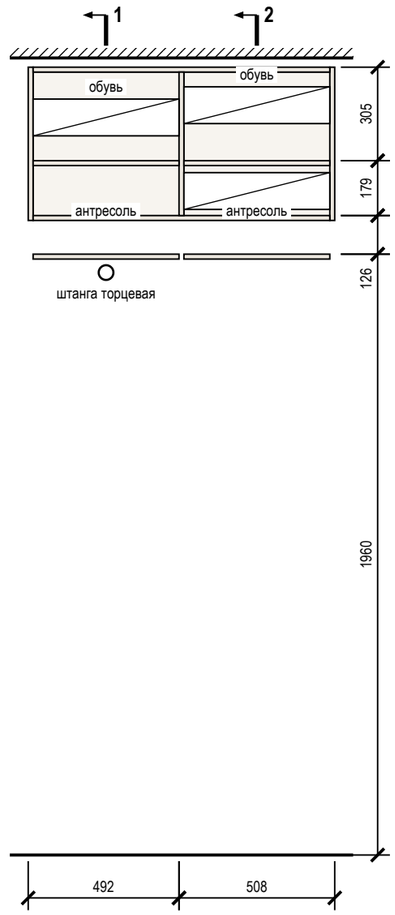

Разрез 1-1

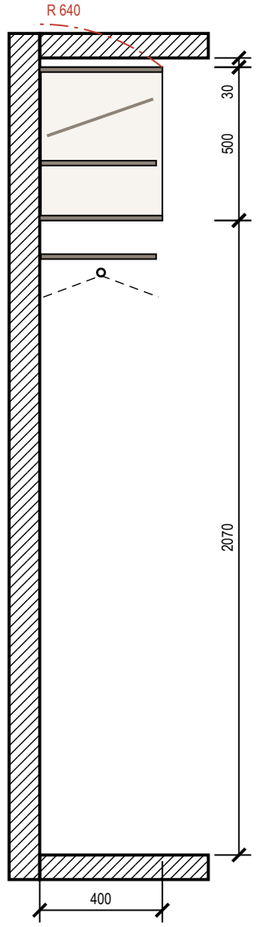

Разрез 2-2

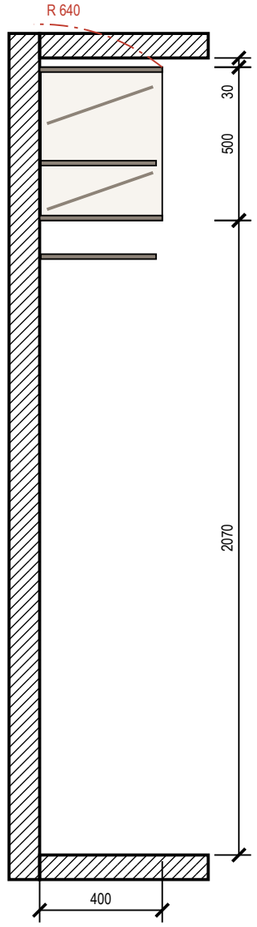

Примечания

1. Размеры — в мм по чистовой отделке; изделие 1000×400×500 (Ш×Г×В). Перед раскроем — контрольный замер цеха после чистовой отделки стен, пола и потолка.
2. Корпус — ЛДСП 16 мм, задняя стенка ХДФ 4 мм в паз, цоколь 0 мм на регулируемых опорах; открытая система без фасадов, ящики с фасадами.
3. Кромка: скрытые торцы 0,4 мм, видимые 2 мм (ПВХ/АБС).
4. Номинальные зазоры: между фасадами ящиков 3 мм, фасад ящика — стойка 2 мм.
5. Ящики — направляющие полного выдвижения NL 350 (внутренняя глубина 396 мм ≥ NL + 3); присадка по 32-й системе — выполняет цех.
6. Зазор до потолка 30 мм — закрыть планкой в цвет корпуса при монтаже.
7. Подъём корпуса (траектория на виде — красная: корпус не проходит под потолком): диагональ боковины √(500² + 400²) = 640 мм > 530 мм до потолка — поднять собранный корпус нельзя: высота корпуса не более 330 мм, остальное — компенсатор, либо сборка стоя на месте.
8. Крепление к стене от опрокидывания: true; основание стены и шаг анкеров — монтажная схема шкафов.

Условные обозначения

- корпус и полки ЛДСП (вид на стену)
- задняя стенка ХДФ
- деталь в разрезе
- штанга для плечиков (на разрезе — плечики 450 мм)
- траектория угла корпуса при подъёме в проектное положение

Допущения и предложения на листе

Основа листа: размеры помещений и положение проёмов введены заказчиком в брифе, на объекте не замерены (К-1); высота потолка 2700 мм — по брифу заказчика, не замерена (К-2); толщины стен приняты по брифу: наружные 200 мм, внутренние 150 мм — не обмерены (К-1); тип дома монолитный, перекрытие 200 мм — по брифу заказчика, документов нет (К-3); планировка (стены, проёмы, объединение кухни и гостиной, расширение санузла) — по брифу без обмера и плана БТИ (К-7); разрешённая мощность 10 кВт принята, ТУ не переданы (К-8); вентканалы приняты, в брифе не заданы (К-9); подрайон климата не задан — принят не северный (жилые от 2,5 м) (К-10).
См. лист открытых вопросов (лист 5, записи К-1–К-3, К-7–К-10).

1000 мм · печать 1:1

Изм.	Кол.уч	Лист	№ док.	Подп.	Дата
Разраб.		Кырлан А.С.			21.10.26
Пров.					
ГИП					
Н. контр.					
Утв.					

ГД-2026-011-АИ

Квартира 56 м²

ЖК «Северный парк», Москва

Дизайн-проект интерьера

Стадия	Лист	Листов
РП	56	83

Система хранения Пр3

М 1:20

Кырлан Александр Сергеевич


выпуск 19.10.2026 № 1c3e34763b · стр. 66 из 117

Кухня (пом. 1). Развёртка гарнитура


Гостиная-кухня (пом. 1) · стена Г · вид из помещения · размеры в мм, отметки в м

ПРЕДВАРИТЕЛЬНО · не для производства работ · открыто пунктов: 10 (реестр — л. 5)


Вид с фасадами

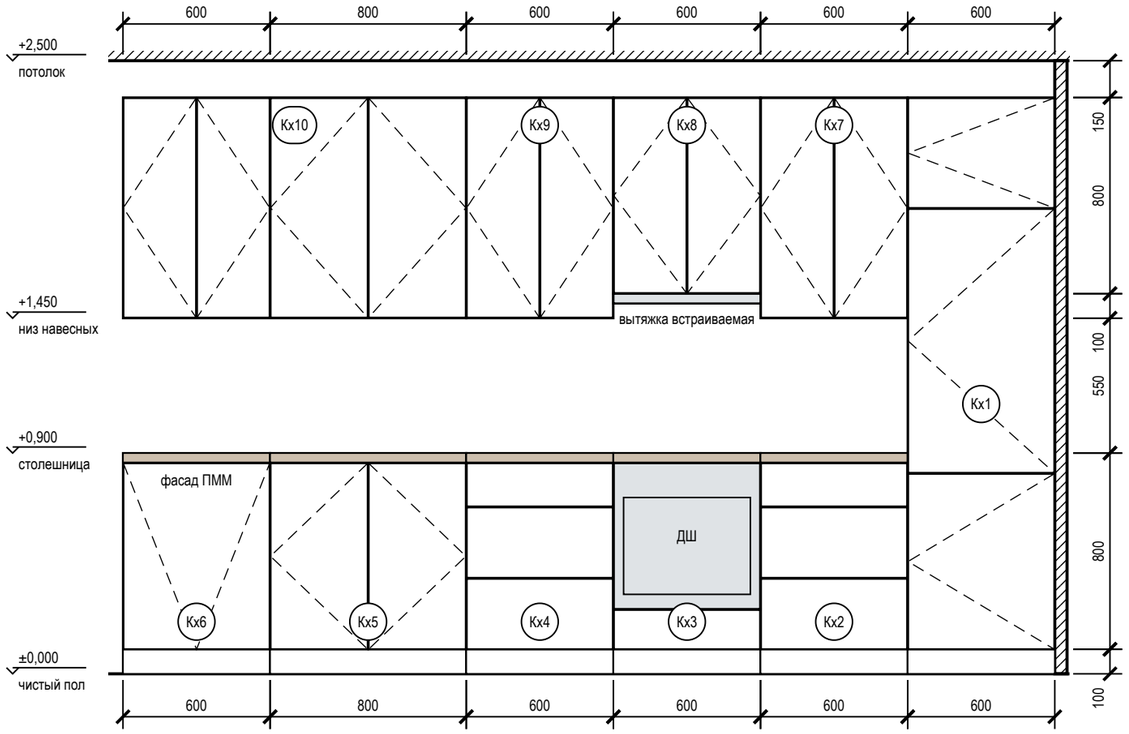


Вид без фасадов (наполнение, выводы)

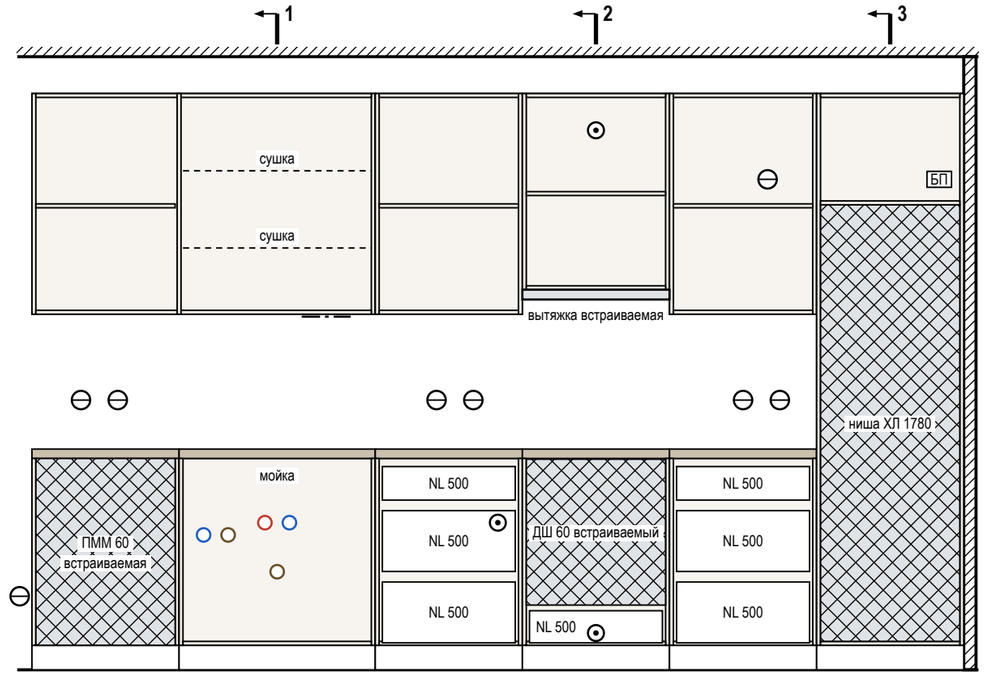


Разрез 1-1

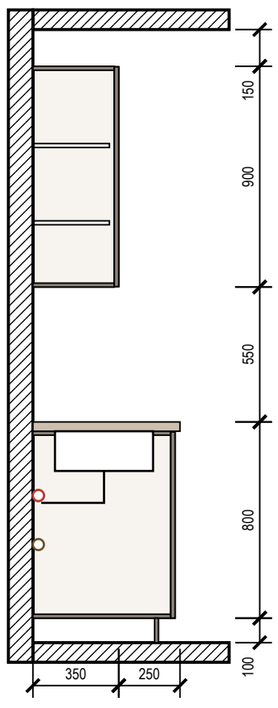

Разрез 2-2

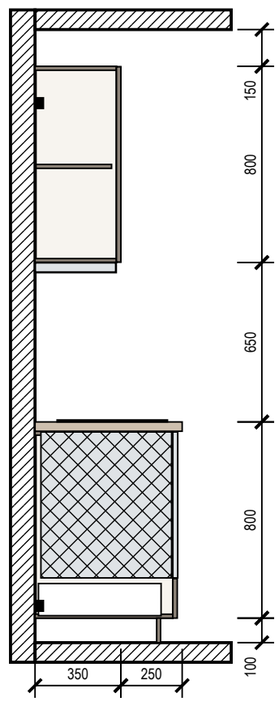

Разрез 3-3

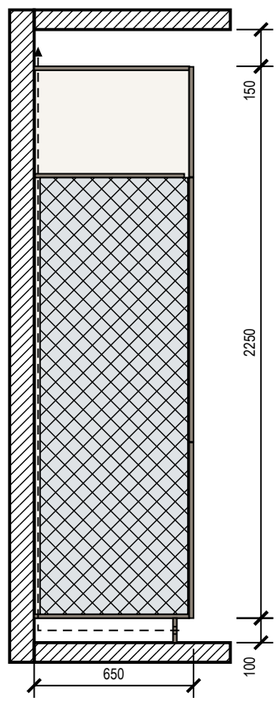

1000 мм · печать 1:1

Условные обозначения

- фасад распашной: линии сходятся к стороне петель
- фасад ящика, карго
- встраиваемая техника
- столешница
- доборная планка
- деталь в разрезе
- К1 — марка модуля
- розетка на стене
- вывод кабеля к технике
- В1 — вывод воды В1 / Т3, канализации К1

Примечания

1. Размеры — в мм по чистовой отделке, вид из помещения; марки — как на плане расстановки. Перед раскроем — контрольный замер цеха после фартука и пола.
2. Корпуса — ЛДСП 16 мм, задняя стенка ХДФ 4 мм; фасады — МДФ, эмаль матовая 18 мм, цвет по колерной карте; столешница 38 мм, свес 20 мм; цоколь 100 мм.
3. Кромка: скрытые торцы 0,4 мм, видимые 2 мм. Номинальные зазоры: между фасадами 3 мм, фасад — столешница 3 мм, фасад — стена не менее 3 мм.
4. Ящики полного выдвижения и петли — с доводчиком; присадка по 32-й системе — выполняет цех.
5. Вытяжка встраивается в навесной модуль над варочной: её низ 610 мм над панелью — меньше 650 мм, модуль поднять или принять вытяжку с допуском по паспорту модели.
6. Ниши техники (холодильник — ориентир 1780 мм) — по монтажным схемам выбранных моделей: решётка в цоколе и канал за пеналом холодильника, зазор за духовым шкафом, фасад ПММ на двери машины.

Допущения и предложения на листе

Основа листа: размеры помещений и положение проёмов введены заказчиком в брифе, на объекте не замерены (К-1); высота потолка 2700 мм — по брифу заказчика, не замерена (К-2); толщины стен приняты по брифу: наружные 200 мм, внутренние 150 мм — не обмерены (К-1); тип дома монолитный, перекрытие 200 мм — по брифу заказчика, документов нет (К-3); планировка (стены, проёмы, объединение кухни и гостиной, расширение санузла) — по брифу без обмера и плана БТИ (К-7); разрешённая мощность 10 кВт принята, ТУ не переданы (К-8); вентканалы приняты, в брифе не заданы (К-9); подрайон климата не задан — принят не северный (жилые от 2,5 м) (К-10).
См. лист открытых вопросов (лист 5, записи К-1–К-3, К-7–К-10).

Изм.	Кол.уч	Лист	№ док.	Подп.	Дата
Разраб.		Кырлан А.С.			21.10.26
Пров.					
ГИП					
Н. контр.					
Утв.					

ГД-2026-011-АИ

Квартира 56 м²

ЖК «Северный парк», Москва

Дизайн-проект интерьера

Стадия	Лист	Листов
РП	57	83

Кухня (пом. 1). Развёртка гарнитура

М 1:25

Кырлан Александр Сергеевич


выпуск 19.10.2026 № 1c3e34763b · стр. 67 из 117

Кухня (пом. 1). Монтажная схема


Гостиная-кухня (пом. 1) · стена Г · размеры в мм от чистых поверхностей, высоты — от чистого пола

ПРЕДВАРИТЕЛЬНО · не для производства работ · открыто пунктов: 10 (реестр — л. 5)

Привязка выводов и крепление модулей

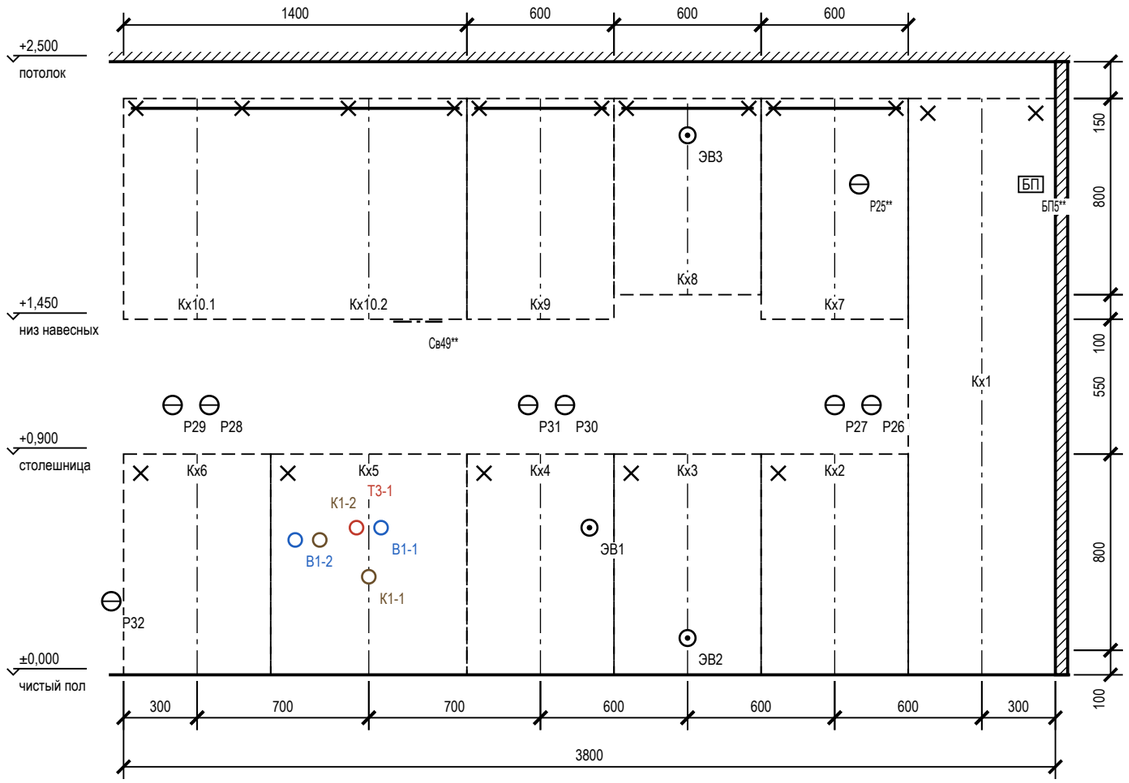

План столешницы

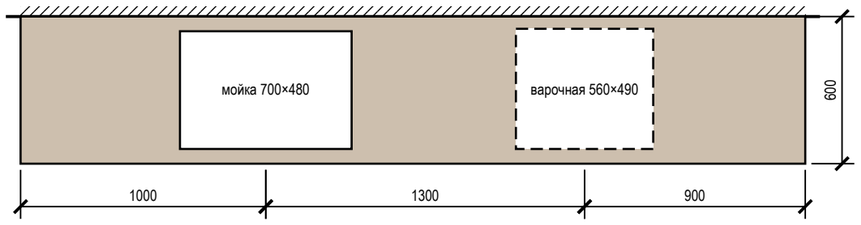

Привязка выводов к осям модулей

Код	Назначение	Модуль	От оси, мм	Н, мм	Размещение
Р32	розетка — посудомоечная машина (на стене за торцом гарнитура, доступ сбоку)			300	вне гарнитура
Р29	розетка — фартук	Кх6	−100	1100	над столешницей (фартук)
Р28	розетка ×2 — фартук	Кх6	+50	1100	над столешницей (фартук)
В1-2	В1 — кран ПММ в шкафу мойки	Кх5	−300	550	в модуле мойки
К1-2	К1 Ø40 — слив ПММ в шкафу мойки	Кх5	−200	550	в модуле мойки
Т3-1	Т3 — межос. 100	Кх5	−50	600	в модуле мойки
К1-1	К1 Ø50 — мойка	Кх5	0	400	в модуле мойки
В1-1	В1 — межос. 100	Кх5	+50	600	в модуле мойки
Св49**	светодиодная лента — подсветка столешницы	Кх5	+200	1440	в профиле по низу навесного модуля
Р31	розетка — фартук между мойкой и варочной	Кх4	−50	1100	над столешницей (фартук)
Р30	розетка ×2 — фартук между мойкой и варочной	Кх4	+100	1100	над столешницей (фартук)
ЭВ1	вывод кабеля — варочная панель (в соседнем модуле Кх4, за ящиком)	Кх4	+200	600	в соседнем модуле, за ящиком
ЭВ2	вывод кабеля — духовой шкаф	Кх3	0	150	под духовым шкафом, доступ через ящик
ЭВ3	вывод кабеля — вытяжка	Кх8	0	2200	в навесном модуле
Р27	розетка — фартук	Кх2	0	1100	над столешницей (фартук)
Р25**	розетка — холодильник (в навесном шкафу Кх7, съёмная панель)	Кх7	+100	2000	в навесном модуле
Р26	розетка ×2 — фартук	Кх2	+150	1100	над столешницей (фартук)
БП5**	блок питания — в пенале М6, верх, съёмная панель	Кх1	+200	2000	над нишей холодильника, съёмная панель

Зазоры под отделку

Поверхность	Отделка	Зазор, мм	Учесть
фартук	керамогранит	10	от чернового основания до корпуса навесных и столешницы
стены	окраска	5	под штукатурку и шпаклёвку за пеналом
пол	инженерная доска		цоколь — после укладки пола, опоры ±20 мм

Условные обозначения

- навесной модуль (невидимый контур)
- ось модуля (от неё — привязка вывода)
- анкер / уголок крепления к стене
- розетка на стене
- вывод кабеля к технике
- B1 — вывод воды В1 / Т3, канализации К1

Примечания

1. Выводы — по проекту электрики и ВК; привязка по горизонтали — от оси модуля (плюс — вправо по виду), по высоте — от чистого пола до оси вывода.
2. Пенал — уголки к стене 2 шт. сверху; нижние модули — стяжками между собой и уголком к стене; ряд выставить по уровню опорами цоколя.
3. Розетки над столешницей — не ниже 150 мм над ней и не за корпусом техники; розетка за ПММ, духовым шкафом и холодильником — только в соседнем модуле или в зоне цоколя с доступом.
4. Столешница — вырезы по шаблонам выбранных моделей мойки и варочной панели; торцы у стены — герметик, пристеночный плинтус.

Допущения и предложения на листе

Основа листа: размеры помещений и положение проёмов введены заказчиком в брифе, на объекте не замерены (К-1); высота потолка 2700 мм — по брифу заказчика, не замерена (К-2); толщины стен приняты по брифу: наружные 200 мм, внутренние 150 мм — не обмерены (К-1); тип дома монолитный, перекрытие 200 мм — по брифу заказчика, документов нет (К-3); планировка (стены, проёмы, объединение кухни и гостиной, расширение санузла) — по брифу без обмера и плана БТИ (К-7); разрешённая мощность 10 кВт принята, ТУ не переданы (К-8); вентканалы приняты, в брифе не заданы (К-9); подрайон климата не задан — принят не северный (жилые от 2,5 м) (К-10).

Знак «**» — предложение проектировщика, заказчиком не утверждено (согласовать с заказчиком): записи в реестре нет: Р25 — высота 2000 мм выше нормы 1 м (ПУЭ 6.6.30) по назначению: питание встроенного холодильника М6, розетка над нишей за съёмной панелью; Св49, БП5 — диммируемость добавлена разработчиком проекта под светорегуляторы S11 и S12.

См. лист открытых вопросов (лист 5, записи К-1–К-3, К-7–К-10).

1000 мм · печать 1:1

Изм.	Кол.уч	Лист	№ док.	Подп.	Дата
Разраб.		Кырлан А.С.			21.10.26
Пров.					
ГИП					
Н. контр.					
Утв.					

ГД-2026-011-АИ

Квартира 56 м²

ЖК «Северный парк», Москва

Дизайн-проект интерьера

Стадия	Лист	Листов
РП	58	83

Кухня (пом. 1). Монтажная схема

М 1:25

Кырлан Александр Сергеевич


выпуск 19.10.2026 № 1c3e34763b · стр. 68 из 117

Шкафы. Монтажная схема


крепление к стене, установочные размеры, зазоры под отделку · размеры в мм

ПРЕДВАРИТЕЛЬНО · не для производства работ · открыто пунктов: 10 (реестр — л. 5)


Шкаф распашной Сп4 (пом. 2)

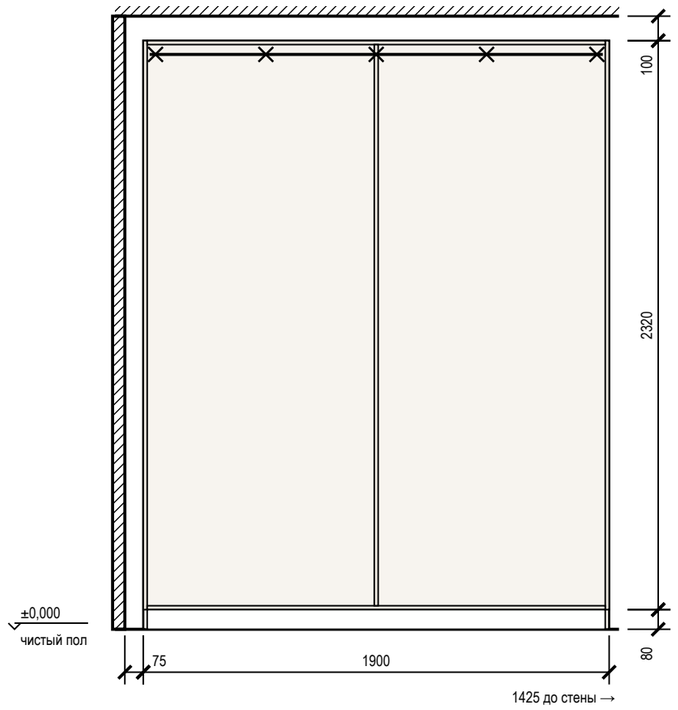


Шкаф распашной Дт2 (пом. 3)

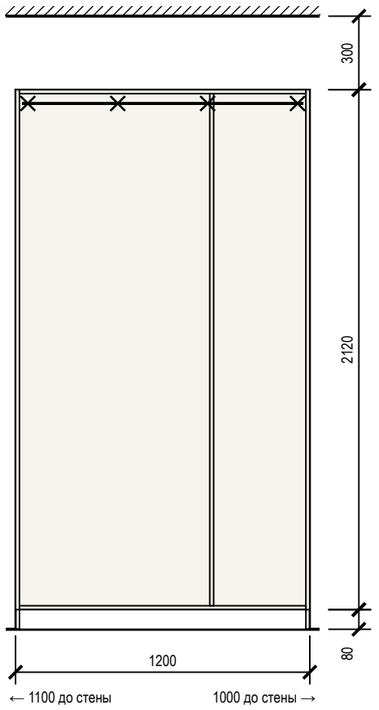

Шкаф-купе Пр1 (пом. 5)

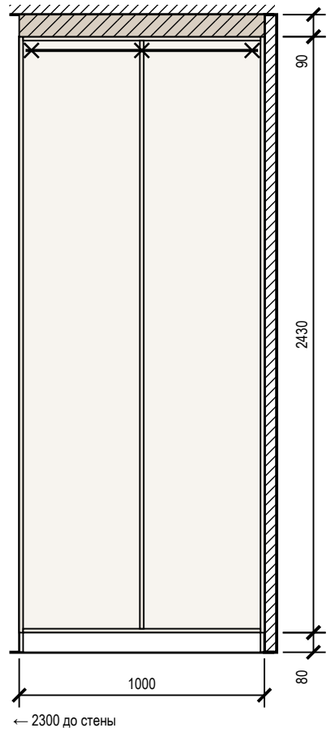

Система хранения Пр3 (пом. 5)

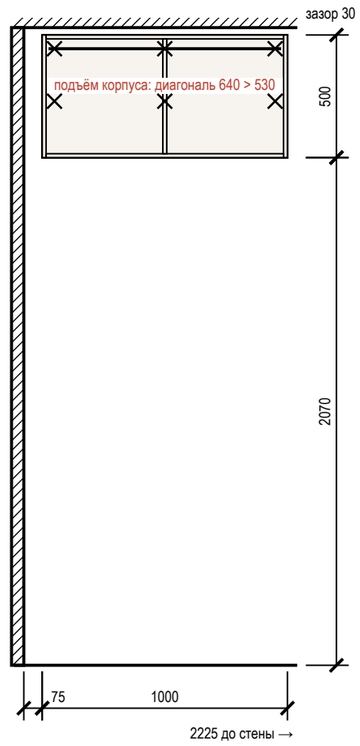

Допущения и предложения на листе

Основа листа: размеры помещений и положение проёмов введены заказчиком в брифе, на объекте не замерены (К-1); высота потолка 2700 мм — по брифу заказчика, не замерена (К-2); толщины стен приняты по брифу: наружные 200 мм, внутренние 150 мм — не обмерены (К-1); тип дома монолитный, перекрытие 200 мм — по брифу заказчика, документов нет (К-3); планировка (стены, проёмы, объединение кухни и гостиной, расширение санузла) — по брифу без обмера и плана БТИ (К-7); разрешённая мощность 10 кВт принята, ТУ не переданы (К-8); вентканалы приняты, в брифе не заданы (К-9); подрайон климата не задан — принят не северный (жилые от 2,5 м) (К-10).

См. лист открытых вопросов (лист 5, записи К-1–К-3, К-7–К-10).

Крепление и зазоры под отделку

Марка	Помещение, стена	Основание	Отделка стены	Зазор, мм	Крепёж по планке	От опрокидывания
Сп4	Спальня (2), стена В	по основанию — см. таблицу крепежа	окраска	5	анкер 5 шт., шаг 450	уголок к стене, 2 шт.
Дт2	Детская (3), стена А	по основанию — см. таблицу крепежа	окраска	5	анкер 4 шт., шаг 367	уголок к стене, 2 шт.
Пр1	Прихожая (5), стена В	по основанию — см. таблицу крепежа	окраска	5	анкер 3 шт., шаг 450	уголки 2 шт.
Пр3	Прихожая (5), стена В	по основанию — см. таблицу крепежа	окраска	5	анкер 6 шт. (2 ряда)	true

Крепёж по основанию стены

Основание стены	Крепёж
бетон, ж/б	анкер-шуруп 7,5×72 или дюбель 8×60 с шурупом 5×70
кирпич полнотелый	дюбель 8×80 с шурупом 5×90
газобетон, пазогребень	дюбель для газобетона 10×100 или химический анкер
гипсокартон	закладная до обшивки (брус 40×80 или фанера 18 мм), саморез в закладную

Условные обозначения

- × — анкер / уголок крепления к стене
- корпус и полки ЛДСП (вид на стену)
- компенсатор — короб до потолка

Примечания

1. Установочные размеры — от чистого пола и чистых стен; перед установкой контрольный замер после отделки.
2. Порядок: корпус выставить по уровню опорами цоколя → закрепить к стене по задней планке → навесить двери и фасады, отрегулировать зазоры → подогнать и закрепить компенсатор.
3. Анкеры — с шагом не более 500 мм, не ближе 50 мм от края планки; на ГКЛ только в закладную, установленную до обшивки.
4. Скрытые коммуникации под анкеры проверить детектором; трассы электрики по плану розеток.

1000 мм · печать 1:1

Изм.	Кол.уч	Лист	№ док.	Подп.	Дата
Разраб.		Кырлан А.С.			21.10.26
Пров.					
ГИП					
Н. контр.					
Утв.					

ГД-2026-011-АИ

Квартира 56 м²

ЖК «Северный парк», Москва

Дизайн-проект интерьера

Стадия	Лист	Листов
РП	59	83

Шкафы. Монтажная схема

М 1:25

Кырлан Александр Сергеевич

выпуск 19.10.2026 № 1c3e34763b · стр. 69 из 117

Ведомости изделий, техники и фурнитуры

встроенная мебель и кухонный гарнитур · размеры в мм

Ведомость изделий

Марка	Наименование	Пом.	Ш×Г×В, мм	Корпус	Фасад	Кромка, мм скр./вид.	Кол.
Сп4	Шкаф распашной	2	1900×600×2400	ЛДСП 16	МДФ 18, эмаль матовая	0,4 / 2	1
Дт2	Шкаф распашной	3	1200×600×2200	ЛДСП 16	МДФ 18, эмаль матовая	0,4 / 2	1
Пр1	Шкаф-купе	5	1000×600×2510	ЛДСП 16	рифлёные панели МДФ в алюминиевом профиле	0,4 / 2	1
Пр3	Система хранения	5	1000×400×500	ЛДСП 16	без фасадов; ящики — МДФ 18, эмаль матовая	0,4 / 2	1
Кх6	Модуль нижний: ПММ	1	600×600×900	ЛДСП 16	МДФ 18, эмаль матовая	0,4 / 2	1
Кх10	Модуль навесной: полки, сушка	1	1400×350×900	ЛДСП 16	МДФ 18, эмаль матовая	0,4 / 2	1
Кх5	Модуль нижний: мойка	1	800×600×900	ЛДСП 16	МДФ 18, эмаль матовая	0,4 / 2	1
Кх4	Модуль нижний: ящики	1	600×600×900	ЛДСП 16	МДФ 18, эмаль матовая	0,4 / 2	1
Кх9	Модуль навесной: полки	1	600×350×900	ЛДСП 16	МДФ 18, эмаль матовая	0,4 / 2	1
Кх3	Модуль нижний: духовой шкаф, варочная	1	600×600×900	ЛДСП 16	МДФ 18, эмаль матовая	0,4 / 2	1
Кх8	Модуль навесной: полки	1	600×350×800	ЛДСП 16	МДФ 18, эмаль матовая	0,4 / 2	1
Кх2	Модуль нижний: ящики	1	600×600×900	ЛДСП 16	МДФ 18, эмаль матовая	0,4 / 2	1
Кх7	Модуль навесной: полки	1	600×350×900	ЛДСП 16	МДФ 18, эмаль матовая	0,4 / 2	1
Кх1	Пенал: холодильник встр.	1	600×650×2350	ЛДСП 16	МДФ 18, эмаль матовая	0,4 / 2	1

Ведомость встраиваемой техники

Поз.	Прибор	Ниша, вырез, мм	Вентиляция	Питание	Схема
Кх6	Посудомоечная машина встраиваемая, 60 см	ниша 600 × 862 (от пола до низа столешницы)	зазор в цоколе, по схеме	розетка в соседнем модуле	по модели
Кх5	Мойка врезная / подстольная с сифоном	вырез по шаблону, ориентир 700 × 480		смеситель — выводы ВК	по модели
Кх3	Духовой шкаф встраиваемый, 60 см	ниша 560 × 595, глубина ≥ 550	зазор за шкафом, вырез в задней стенке	вывод кабеля под шкафом	по модели
Кх3	Варочная панель индукционная, 60 см	вырез в столешнице 560 × 490		вывод кабеля под модулем	по модели
Кх1	Холодильник встраиваемый, ниша 1780	ниша 1780 × 560 × 550	решётка в цоколе, канал за корпусом, выход сверху	розетка над нишей или в соседнем модуле	по модели
Кх3	Вытяжка настенная, 60 см	низ ≥ 650 над панелью	воздуховод к вентканалу, короб до потолка	вывод кабеля в коробе	по модели

Ведомость фурнитуры

№	Фурнитура	Тип, размер	Изделия	Кол.
1	Петля накладная 110° с доводчиком	чашка 35 мм	Сп4, Дт2, Кх10, Кх5, Кх9, Кх8, Кх7, Кх1	73
2	Полкодержатель с фиксацией	ø5 мм	Сп4, Дт2, Пр1, Пр3, Кх10, Кх9, Кх8, Кх7, Кх1	112
3	Штанга овальная 30×15, L = 926	+ 2 держателя	Сп4	1
4	Опора регулируемая с цоколем на клипсах	ход 20 мм	Сп4, Дт2, Пр1	20
5	Анкер по основанию стены	по таблице крепежа	Сп4, Дт2, Пр1, Пр3, Кх10, Кх9, Кх8, Кх7	28
6	Уголок крепления к стене от опрокидывания	стальной	Сп4, Дт2, Пр1, Пр3, Кх1	10
7	Штанга овальная 30×15, L = 776	+ 2 держателя	Дт2	1
8	Система дверей купе: профиль, направляющие, ролики	на 2 двери	Пр1	1
9	Ручка-профиль вертикальная	в цвет профиля	Пр1	2
10	Штанга овальная 30×15, L = 476	+ 2 держателя	Пр1	1
11	Полка для обуви выдвижная наклонная	ширина 476	Пр1, Пр3	6
12	Штанга выдвижная торцевая	L по глубине	Пр3	1
13	Ручка-профиль	латунь матовая	Кх6, Кх10, Кх5, Кх4, Кх9, Кх3, Кх8, Кх2, Кх7, Кх1	23
14	Опора кухонная регулируемая 100–120 мм	+ клипса цоколя	Кх6, Кх5, Кх4, Кх3, Кх2, Кх1	26
15	Комплект навески фасада ПММ	из поставки машины	Кх6	1
16	Сушка для посуды в шкаф	ширина 800	Кх10	1
17	Навес регулируемый для навесного шкафа	пара на секцию	Кх10, Кх9, Кх8, Кх7	5
18	Шина монтажная	L = 1340	Кх10	1
19	Направляющие полного выдвижения с доводчиком NL 500	пара	Кх4, Кх3, Кх2	7
20	Шина монтажная	L = 540	Кх9, Кх8, Кх7	3

Примечания

1. Модели техники выбирает заказчик до изготовления мебели; ниши, вырезы и вентиляция — по монтажной схеме выбранной модели (условие гарантии), её номер вносится в ведомость.
2. Количество фурнитуры — по чертежам изделий; запас крепежа 5 %. Аналоги — по характеристикам (доводчик, нагрузка, ход).
3. Цвет корпусов, фасадов и профилей — по колерной карте проекта.

Допущения и предложения на листе

Основа листа: размеры помещений и положение проёмов введены заказчиком в брифе, на объекте не замерены (К-1); высота потолка 2700 мм — по брифу заказчика, не замерена (К-2); толщины стен приняты по брифу: наружные 200 мм, внутренние 150 мм — не обмерены (К-1); тип дома монолитный, перекрытие 200 мм — по брифу заказчика, документов нет (К-3); планировка (стены, проёмы, объединение кухни и гостиной, расширение санузла) — по брифу без обмера и плана БТИ (К-7); разрешённая мощность 10 кВт принята, ТУ не переданы (К-8); вентканалы приняты, в брифе не заданы (К-9); подрайон климата не задан — принят не северный (жилые от 2,5 м) (К-10).
См. лист открытых вопросов (лист 5, записи К-1–К-3, К-7–К-10).

Изм.	Кол.уч	Лист	№ док.	Подп.	Дата
Разраб.		Кырлан А.С.			21.10.26
Пров.					
ГИП					
Н. контр.					
Утв.					

ГД-2026-011-АИ

Квартира 56 м²

ЖК «Северный парк», Москва

Дизайн-проект интерьера

Стадия	Лист	Листов
РП	60	83

Ведомости изделий, техники и фурнитуры

М б/м

Кырлан Александр Сергеевич

выпуск 19.10.2026 № 1c3e34763b · стр. 70 из 117

09

Развёртки и узлы



Кырлан Александр Сергеевич

выпуск 19.10.2026 · 1c3e34763b · стр. 71 из 117

Реестр марок отделки и позиций альбома

Реестр марок отделки (О ↔ позиции колерной карты) и марки позиций по видам

Реестр марок отделки альбома

Марка	Поверхность	Материал, изделие	Цвет, код	Помещения	Колер. карта
О1	стены	окраска, Tikkurila Euro Power 7, колеровка по NCS, матовая, подготовка Q3	NCS S 0804-Y30R «S 0804-Y30R»	1, 2, 3, 5	К1
О2	фартук	керамогранит, 1200×600×9 мм, аналог: керамогранит под травертин, матовый, затирка CG2WA		1	КМ2
О3	акцентная стена	окраска, Farrow & Ball Modern Emulsion, матовая, подготовка Q3	Farrow & Ball No. 298 «Bancha»	1	К2
О4	плинтус	плинтус МДФ, h 80 мм, аналог: плинтус МДФ под покраску 80×16	NCS S 0804-Y30R «S 0804-Y30R»	1, 2, 5	К4
О5	потолок	окраска, Tikkurila Euro Power 7, глубокоматовая, подготовка Q3	Tikkurila F485 «Damask»	1, 2, 3, 4, 5	К3, К9
О6	пол	инженерная доска, Coswick Классическая, 2100×127 мм, 1167-1101		1, 2, 3	КМ1
О7	акцентная стена	окраска, Tikkurila Euro Power 7, колеровка по NCS, матовая, подготовка Q3	NCS S 5010-G70Y «S 5010-G70Y»	2	К5
О8	акцентная стена	окраска, Tikkurila Euro Power 7, матовая, подготовка Q3	Tikkurila X447 «Sea Smoke»	3	К6
О9	плинтус	плинтус МДФ, Orac Decor Contour (Luxxus), h 69 мм, SX165	NCS S 0804-Y30R «S 0804-Y30R»	3	К7
О10	стены	облицовка плиткой, Atlas Concorde Marvel Travertine, 600×1200×9 мм, A8UZ, затирка CG2WA	Atlas Concorde A8UZ «Marvel Travertine»	4	К8
О11	пол	керамогранит, Atlas Concorde Marvel Travertine, 600×1200×9 мм, A8UZ, затирка CG2WA	Atlas Concorde A8UZ «Marvel Travertine»	4, 5	К8

Марки позиций альбома по видам

Префикс	Что обозначает, позиции	Листы
Д	двери: Д-1–Д-5	13–15
ОК	окна: ОК-1–ОК-3	13–15
Гс, Дт, Кх, Пр, Сп	мебель и оборудование: Гс1–Гс5, Дт1–Дт5, Кх1–Кх11, Пр1–Пр3, Сп1–Сп6	16–20
П, Сн	сантехнические приборы: П1, П2, Сн1–Сн5	31–33
ДК	декор (картины, зеркала, растения): ДК1–ДК8	1, 47–51
Т	текстиль (шторы, ковры): Т1–Т14, Т16–Т19	1, 47–51
S	выключатели: S1–S10, S11**, S12**, S13, S15	21–28
Р	розетки: Р1–Р6, Р7**, Р8**, Р9–Р11, Р13–Р16, Р17**, Р18**, Р19**, Р20–Р24, Р25**, Р26–Р32	21–28
ТВ	розетки ТВ: ТВ1	21–28
LAN	розетки компьютерные: LAN1–LAN3	21–28
ЭВ	выводы кабеля: ЭВ1–ЭВ3, ЭВ4**, ЭВ6**	21–28
АР	точки доступа Wi-Fi: АР1**, АР2**	21–28
Св	светильники: Св1–Св15, Св17–Св38, Св41, Св42**, Св43**, Св44**, Св45–Св48, Св49**	21–28
БП	блоки питания LED: БП1–БП4, БП5**	21–28
ИП	извещатели: ИП1–ИП5	21–28

Марки позиций альбома по видам (продолжение)

Префикс	Что обозначает, позиции	Листы
КУП	электроустановочные изделия: КУП1**	21–28
ЩК, ЩС**	щиты: ЩК, ЩС**	21–28
ДФ	домофон: ДФ1	21–28
Ст В1, Ст К1	стояки (системы В1, Т3, К1): Ст В1-1*, Ст К1-1*	31–33
О	марки отделки (реестр альбома): О1–О11	2–4, 61–75
К, КМ	позиции колерной карты: К1–К9, КМ1, КМ2	45, 46
РО	радиаторы отопления: РО-1–РО-3	29, 30

Примечания

1. Марка отделки О — одна на весь альбом: одна и та же отделка (материал, изделие, цвет, формат) на всех листах имеет одну марку; на развёртках и планах стоят марки этого реестра.
2. Столбец «Колер. карта» — позиции колерной карты (лист 45): К — окраска по коду цвета, КМ — материал без кода цвета; «Помещения» — номера по экспликации; количества — по ведомости отделки помещений (лист 44).
3. Марки позиций: один префикс — один вид позиций на весь альбом (двери Д, окна ОК, мебель М, сантехприборы П, декор ДК, текстиль Т, колерная карта К и КМ, радиаторы РО, розетки Р, выключатели S, светильники Св; стояки — «Ст» и система, например «Ст К1-1*»). Совпадение префиксов у разных видов — замечание к исходным данным, при выпуске исправляется в модели.

Допущения и предложения на листе. Основа листа: размеры помещений и положение проёмов введены заказчиком в брифе, не замерены (К-1); высота потолка 2700 мм — по брифу заказчика, не замерена (К-2); толщины стен приняты по брифу: наружные 200 мм, внутренние 150 мм — не обмерены (К-1); тип дома монолитный, перекрытие 200 мм — по брифу заказчика, документов нет (К-3); планировка (стены, проёмы, объединение кухни и гостиной, расширение санузла) — по брифу без обмера и плана БТИ (К-7); разрешённая мощность 10 кВт принята, ТУ не переданы (К-8); вентканалы приняты, в брифе не заданы (К-9); подрайон климата не задан — принят не северный (жилые от 2,5 м) (К-10). Знак «*» — принято, не замерено (замерить): К-4: Ст К1-1, Ст В1-1. Знак «**» — предложено, не утверждено (согласовать): записи в реестре нет: плинтус пом. 1, 2, 5, фартук пом. 1, S11, S12, Р18, Р19, Р25, Св42, Св43, Св44, Св49, БП5, Р7, Р8, ЭВ4, КУП1, ЭВ6, Р17, АР2, ЩС, АР1. См. лист открытых вопросов (лист 5, записи К-1–К-4, К-7–К-10).


						ГД-2026-011-АИ	
						Квартира 56 м² ЖК «Северный парк», Москва	
Изм.	Кол.уч	Лист	№ док.	Подп.	Дата	Дизайн-проект интерьера	Стадия: РП; Лист: 61; Листов: 83
Разраб.		Кырлан А.С.			21.10.26		
Пров.							
ГИП							
Н. контр.						**Реестр марок отделки и позиций альбома** М б/м	**Кырлан Александр Сергеевич**
Утв.							

выпуск 19.10.2026 № 1c3e34763b · стр. 72 из 117

Схема расположения развёрток и узлов

План квартиры: марки развёрток по помещениям, выноски узлов, ведомость «марка → лист»

ПРЕДВАРИТЕЛЬНО · не для производства работ · открыто пунктов: 10 (реестр — л. 5)

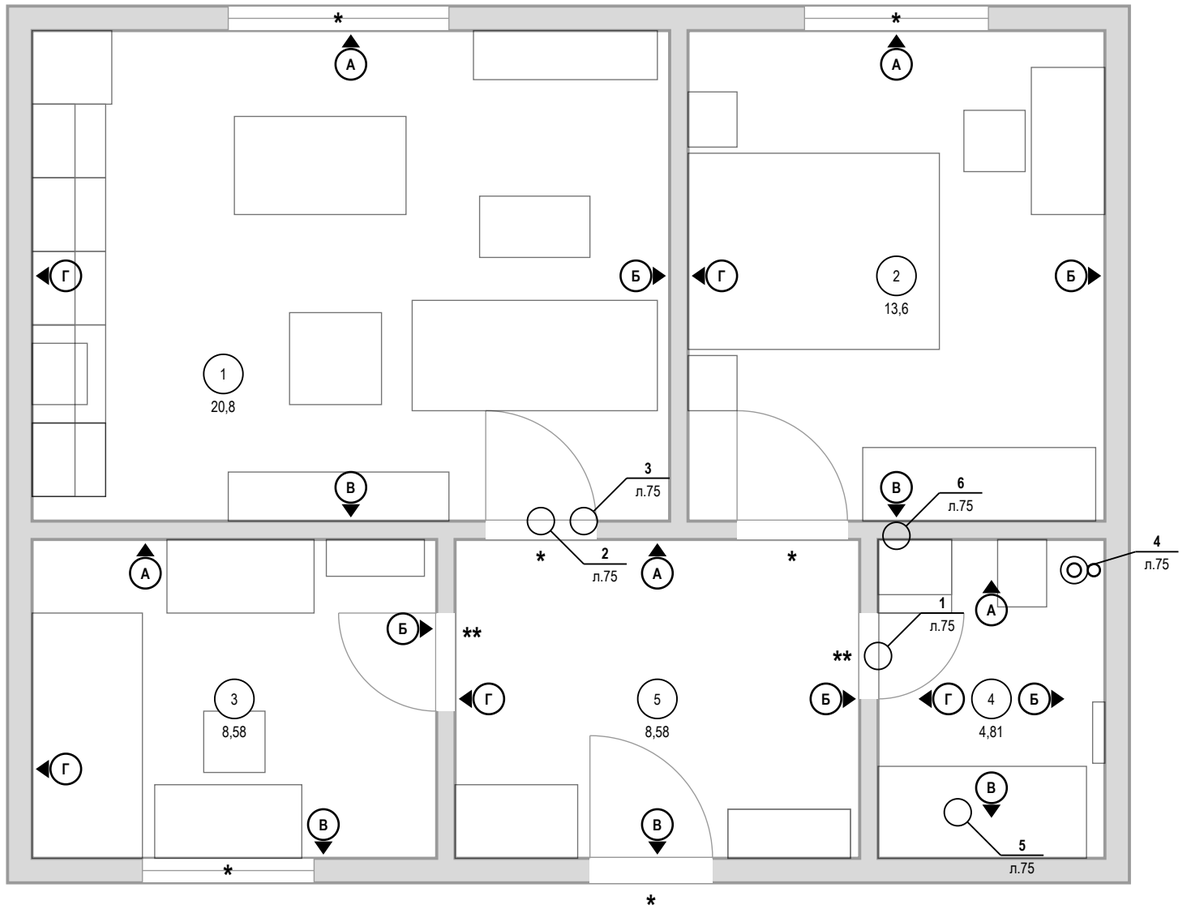

Развёртки и узлы: марка → лист

Марка	Помещение / узел	Лист
Г	Гостиная-кухня (пом. 1)	63
А, Б	Гостиная-кухня (пом. 1)	64
В	Гостиная-кухня (пом. 1)	65
А, Б	Спальня (пом. 2)	66
В, Г	Спальня (пом. 2)	67
А, Б	Детская (пом. 3)	68
В, Г	Детская (пом. 3)	69
А	Санузел (пом. 4)	70
Б, В	Санузел (пом. 4)	71
Г	Санузел (пом. 4)	72
А, Б	Прихожая (пом. 5)	73
В, Г	Прихожая (пом. 5)	74
узел 1	Порог 15 мм: мокрая зона — жилое помещение	75
узел 2	Стык покрытий пола Т-профилем без перепада	75
узел 3	Дверь скрытого монтажа в плоскости стены, плинтус	75
узел 4	Короб стояков К1-1 с люком и звукоизоляцией	75
узел 5	Гидроизоляция санузла: заход на стены 200 мм, примыкание ванны	75
узел 6	Плинтус МДФ 80×16 мм у окрашенной стены	75

Допущения и предложения на листе. Основа листа: размеры помещений и положение проёмов введены заказчиком в брифе, на объекте не замерены (К-1); высота потолка 2700 мм — по брифу заказчика, не замерена (К-2); толщины стен приняты по брифу: наружные 200 мм, внутренние 150 мм — не обмерены (К-1); тип дома монолитный, перекрытие 200 мм — по брифу заказчика, документов нет (К-3); планировка (стены, проёмы, объединение кухни и гостиной, расширение санузла) — по брифу без обмера и плана БТИ (К-7); разрешённая мощность 10 кВт принята, ТУ не переданы (К-8); вентканалы приняты, в брифе не заданы (К-9); подрайон климата не задан — принят не северный (жилые от 2,5 м) (К-10). Знак «*» — принято, не замерено и не подтверждено (замерить на объекте): К-4: Ст К1-1 — положение стояка канализации — по брифу заказчика, не замерено; Ст В1-1 — положение стояка холодной воды — по брифу заказчика, не замерено. Знак «**» — предложение проектировщика, заказчиком не утверждено (согласовать с заказчиком). См. лист открытых вопросов (лист 5, записи К-1–К-5, К-7–К-10).

Условные обозначения

- А — марка развёртки: буква стены, стрелка — взгляд
- выноска узла: над полкой — узел, под полкой — лист
- 1 — номер помещения, площадь м²

1000 мм · печать 1:1

Примечания

1. Развёртки — вид на стену изнутри помещения; буквы стен — одна система на весь альбом (как на листах выводов, плитки и отделки).
2. Стены без электроточек, мебели, декора и акцентной отделки развёрток не имеют: их отделка — по ведомости отделки помещений.
3. Узлы — на листе узлов; места применения — по выноскам этого листа и ведомости «марка → лист».

Изм.	Кол.уч	Лист	№ док.	Подп.	Дата
Разраб.		Кырлан А.С.			21.10.26
Пров.					
ГИП					
Н. контр.					
Утв.					

ГД-2026-011-АИ

Квартира 56 м²

ЖК «Северный парк», Москва

Дизайн-проект интерьера

Стадия	Лист	Листов
РП	62	83

Схема расположения развёрток и узлов

М 1:50

Кырлан Александр Сергеевич

выпуск 19.10.2026 № 1c3e34763b · стр. 73 из 117

Развёртка стены Г. Гостиная-кухня (пом. 1), кухонный фронт

Гостиная-кухня (пом. 1) · вид изнутри помещения · размеры в мм, отметки в м

ПРЕДВАРИТЕЛЬНО · не для производства работ · открыто пунктов: 10 (реестр — л. 5)

Развёртка стены Г


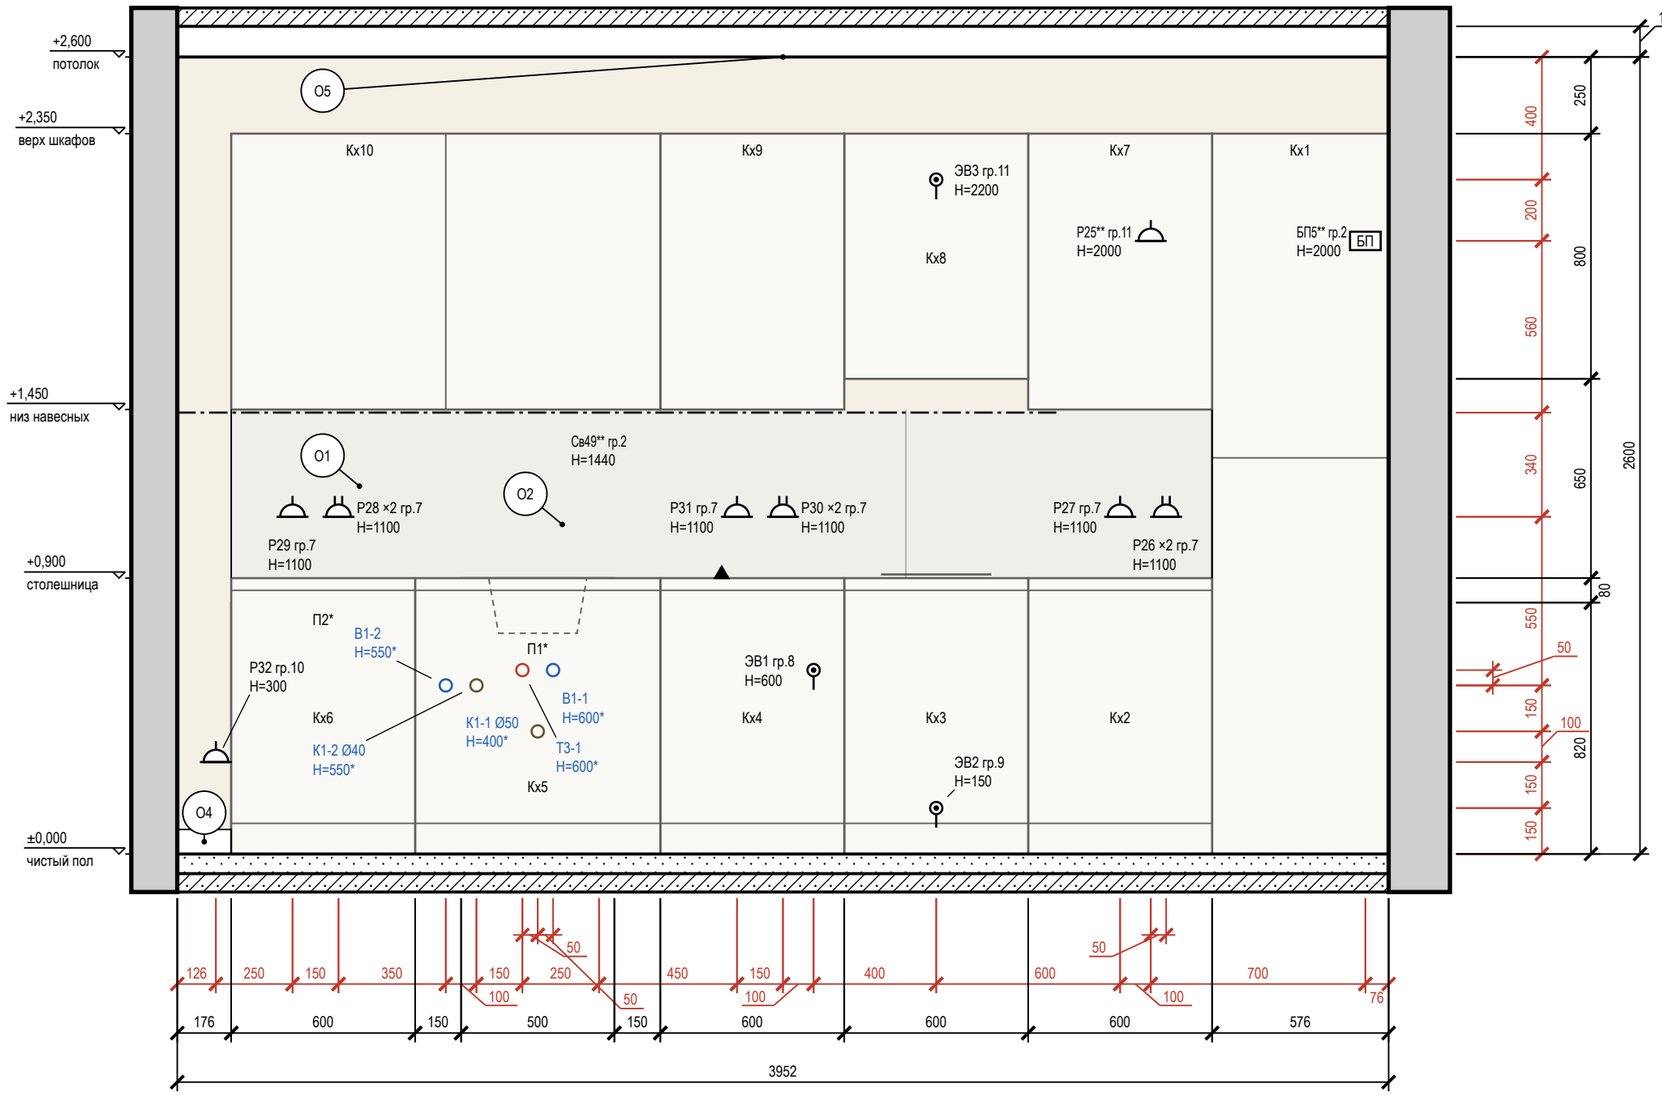


Схема развёрток (М 1:100)

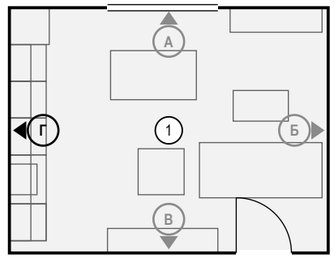

Условные обозначения

- розетка с заземляющим контактом; у знака — марка, ×N постов в рамке, гр. — группа щита, H — высота оси, мм
- вывод кабеля для подключения прибора (без розетки), марка ЭВ
- светодиодная лента в профиле / в карнизе короба
- БП — блок питания LED, с доступом (люк от 100×100 мм)
- вывод В1 (код — в ведомости привязок)
- вывод Т3 (код — в ведомости привязок)
- вывод К1 (код — в ведомости привязок)
- привязки точек и выводов от угла и от пола, мм
- мебель и приборы — фасад по расстановке (условно)
- стены и перекрытия в сечении
- плитка: сетка швов по формату, ▲ — ось старта
- окраска: тон — цвет по коду производителя (условно)
- О1 — марка отделки по реестру отделки альбома
- А — марка развёртки: буква стены, стрелка — взгляд

Допущения и предложения на листе. Основа листа: размеры помещений и положение проёмов введены заказчиком в брифе, не замерены (К-1); высота потолка 2700 мм — по брифу заказчика, не замерена (К-2); толщины стен приняты по брифу: наружные 200 мм, внутренние 150 мм — не обмерены (К-1); тип дома монолитный, перекрытие 200 мм — по брифу заказчика, документов нет (К-3); планировка (стены, проёмы, объединение кухни и гостиной, расширение санузла) — по брифу без обмера и плана БТИ (К-7); разрешённая мощность 10 кВт принята, ТУ не переданы (К-8); вентканалы приняты, в брифе не заданы (К-9); подрайон климата не задан — принят не северный (жилые от 2,5 м) (К-10). Знак «*» — принято, не замерено (замерить): К-1: окно пом. 1 (стена А), дверь пом. 1 (стена В). Знак «**» — предложено, не утверждено (согласовать): записи в реестре нет: Р25, Св49, БП5. См. лист открытых вопросов (лист 5, записи К-1–К-3, К-7–К-10).

Примечания

1. Развёртки — вид на стену изнутри помещения, по часовой стрелке; расположение — на схеме листа и на листе 62; размеры — в мм по чистовым поверхностям; отметки — в м от ±0,000; высоты H — от чистого пола помещения до оси изделия, у декора — до центра.
2. Красные цепочки — привязки электроточек и выводов: по горизонтали от угла чистовых стен, по вертикали от чистого пола, до оси изделия; звенья короче 3 мм на листе вынесены во второй ярус (ближняя к стене цепочка).
3. У знака электроточки: марка (Р — розетка, S — выключатель, Св — светильник, ЭВ — вывод кабеля), ×N — число постов в рамке, гр. — группа щита, H — высота оси от чистого пола, мм; группы по клавишам выключателя — на листе выключателей.
4. Схема мебели, приборов и декора не является технической документацией для производства мебели; габариты — по паспортам изделий (* — высота не задана в проекте, показана по типовому изделию).
5. Выводы ВК — коды и высоты по листу выводов сантехники; * — высота принята по типовой практике монтажа, окончательно — по паспорту прибора.
6. Выводы кухонной техники — по утверждённому проекту кухни: привязки выводов даются от осей модулей гарнитура.
7. Потолок на развёртках — по нижнему уровню У2; другие уровни потолка помещения: У1 +2,600.

1000 мм · печать 1:1

Изм.	Кол.уч	Лист	№ док.	Подп.	Дата
Разраб.		Кырлан А.С.			21.10.26
Пров.					
ГИП					
Н. контр.					
Утв.					

ГД-2026-011-АИ

Квартира 56 м²

ЖК «Северный парк», Москва

Дизайн-проект интерьера

Стадия	Лист	Листов
РП	63	83

Развёртка стены Г. Гостиная-кухня (пом. 1), кухонный фронт

М 1:20

Кырлан Александр Сергеевич


выпуск 19.10.2026 № 1c3e34763b · стр. 74 из 117

Развёртки стен А, Б. Гостиная-кухня (пом. 1)

Гостиная-кухня (пом. 1) · вид изнутри помещения · размеры в мм, отметки в м

ПРЕДВАРИТЕЛЬНО · не для производства работ · открыто пунктов: 10 (реестр — л. 5)

Развёртка стены А

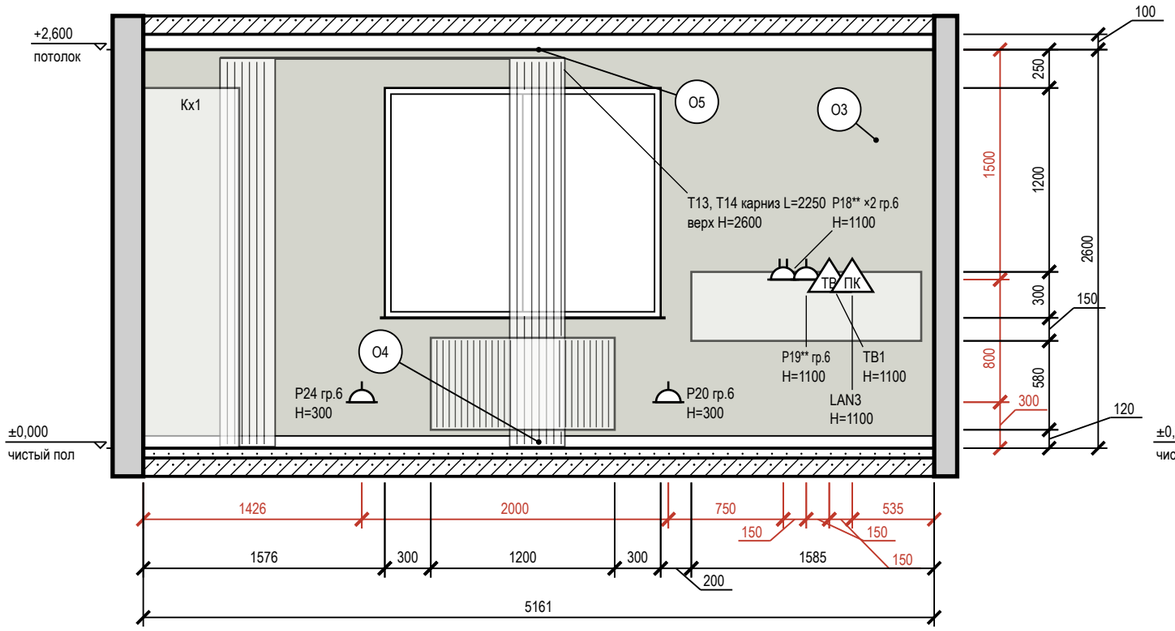

Развёртка стены Б


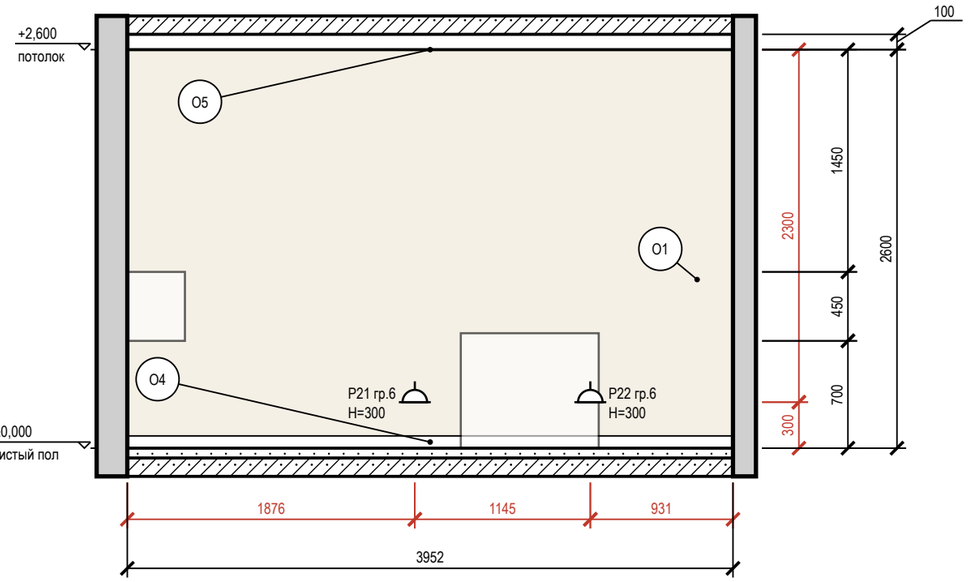


Схема развёрток (М 1:100)

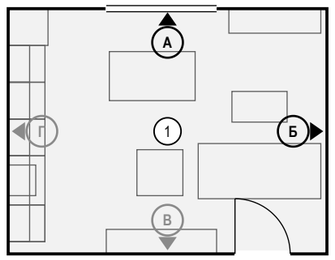

Условные обозначения

- розетка с заземляющим контактом; у знака — марка, ×N постов в рамке, гр. — группа щита, Н — высота оси, мм
- ПК — розетка компьютерная RJ45
- ТВ — розетка телевизионная
- привязки точек и выводов от угла и от пола, мм
- мебель и приборы — фасад по расстановке (условно)
- карниз (шина) и шторы в собранном виде: марка Т, длина L, верх Н
- окно: проём, рама, подоконник
- радиатор отопления; марка — по плану отопления
- стены и перекрытия в сечении
- окраска: тон — цвет по коду производителя (условно)
- О1 — марка отделки по реестру отделки альбома
- А — марка развёртки: буква стены, стрелка — взгляд

Ведомость отделки (на листе)

Марка	Поверхность	Материал, изделие	Цвет, код	Кол.
О1	стены	окраска, Tikkurila Euro Power 7, колеровка по NCS, матовая, подготовка Q3	NCS S 0804-Y30R «S 0804-Y30R»	10,3 м²
О3	акцентная стена	окраска, Farrow & Ball Modern Emulsion, матовая, подготовка Q3	Farrow & Ball No. 298 «Bancha»	10,7 м²
О4	плинтус	плинтус МДФ, h 80 мм, аналог: плинтус МДФ под покраску 80×16	NCS S 0804-Y30R «S 0804-Y30R»	9,1 м
О5	потолок	окраска, Tikkurila Euro Power 7, глубокоматовая, подготовка Q3	Tikkurila F485 «Damask»	20,8 м²

Допущения и предложения на листе

Основа листа: размеры помещений и положение проёмов введены заказчиком в брифе, на объекте не замерены (К-1); высота потолка 2700 мм — по брифу заказчика, не замерена (К-2); толщины стен приняты по брифу: наружные 200 мм, внутренние 150 мм — не обмерены (К-1); тип дома монолитный, перекрытие 200 мм — по брифу заказчика, документов нет (К-3); планировка (стены, проёмы, объединение кухни и гостиной, расширение санузла) — по брифу без обмера и плана БТИ (К-7); разрешённая мощность 10 кВт принята, ТУ не переданы (К-8); вентканалы приняты, в брифе не заданы (К-9); подрайон климата не задан — принят не северный (жилые от 2,5 м) (К-10).

Знак «*» — принято, не замерено и не подтверждено (замерить на объекте): К-1: окно пом. 1 (стена А) — окно: положение, ширина, высота и подоконник — по брифу заказчика, не замерены; ограждение 900 мм — предложение исполнителя; дверь пом. 1 (стена В) — проём в существующей стене между пом. 1 и 5: положение и ширина — по брифу заказчика, не замерены.

Знак «**» — предложение проектировщика, заказчиком не утверждено (согласовать с заказчиком): записи в реестре нет: Р18 — высота 1100 мм выше нормы 1 м (ПУЭ 6.6.30) по назначению: питание ТВ, в одной зоне с выводами ТВ1 и LAN3; Р19 — высота 1100 мм выше нормы 1 м (ПУЭ 6.6.30) по назначению: питание приставки ТВ, в одной зоне с выводами ТВ1 и LAN3.

См. лист открытых вопросов (лист 5, записи К-1–К-3, К-7–К-10).

Примечания

1. Развёртки — вид на стену изнутри помещения, по часовой стрелке; расположение — на схеме листа и на листе 62; размеры — в мм по чистовым поверхностям; отметки — в м от ±0,000; высоты Н — от чистого пола помещения до оси изделия, у декора — до центра.
2. Красные цепочки — привязки электроточек и выводов: по горизонтали от угла чистовых стен, по вертикали от чистого пола, до оси изделия; звенья короче 3 мм на листе вынесены во второй ярус (ближняя к стене цепочка).
3. У знака электроточки: марка (Р — розетка, S — выключатель, Св — светильник, ЭВ — вывод кабеля), ×N — число постов в рамке, гр. — группа щита, Н — высота оси от чистого пола, мм; группы по клавишам выключателя — на листе выключателей.
4. Схема мебели, приборов и декора не является технической документацией для производства мебели; габариты — по паспортам изделий (* — высота не задана в проекте, показана по типовому изделию).
5. Карнизы (шины) — по ведомости текстиля декоратора; длина L и верх Н — по развёртке, крепление — до окраски потолка.
6. Потолок на развёртках — по нижнему уровню У2; другие уровни потолка помещения: У1 +2,600.
7. Линии узора (швы плитки, складки штор, рёбра радиаторов) прерываются у знаков и выносок — просвет между линиями не менее 0,7 мм.

1000 мм · печать 1:1

Изм.	Кол.уч	Лист	№ док.	Подп.	Дата
Разраб.		Кырлан А.С.			21.10.26
Пров.					
ГИП					
Н. контр.					
Утв.					

ГД-2026-011-АИ

Квартира 56 м²

ЖК «Северный парк», Москва

Дизайн-проект интерьера

Стадия	Лист	Листов
РП	64	83

Развёртки стен А, Б. Гостиная-кухня (пом. 1)

М 1:40

Кырлан Александр Сергеевич

выпуск 19.10.2026 № 1c3e34763b · стр. 75 из 117

Развёртка стены В. Гостиная-кухня (пом. 1)

Гостиная-кухня (пом. 1) · вид изнутри помещения · размеры в мм, отметки в м

ПРЕДВАРИТЕЛЬНО · не для производства работ · открыто пунктов: 10 (реестр — л. 5)

Развёртка стены В


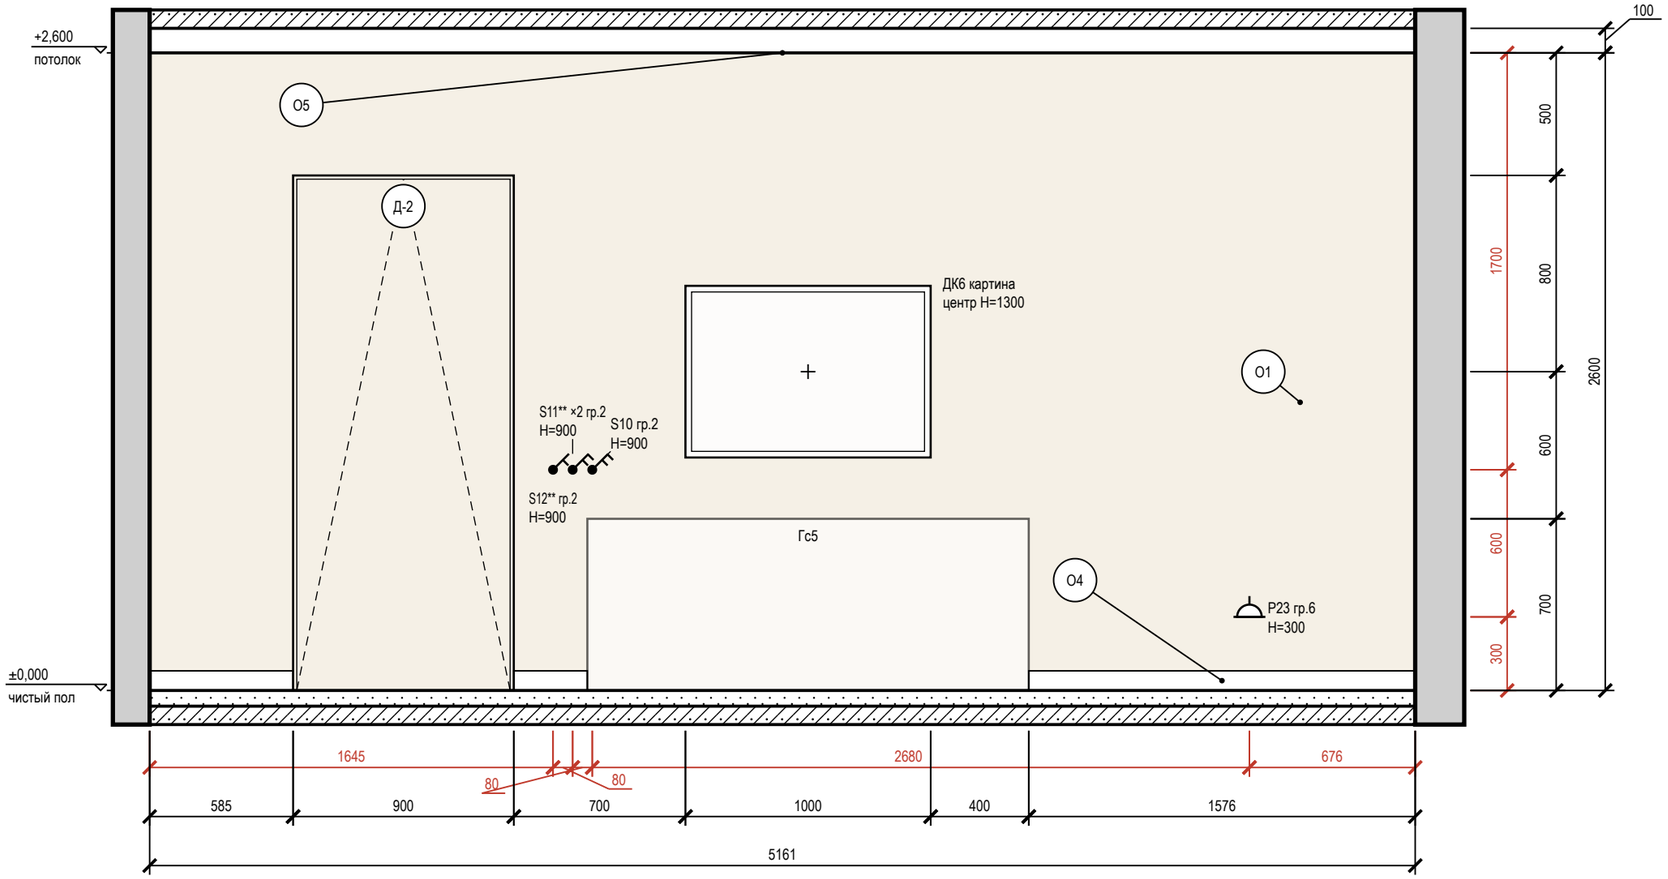


Схема развёрток (М 1:100)

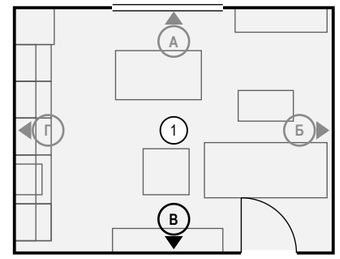

Условные обозначения

- розетка с заземляющим контактом; у знака — марка, ×N постов в рамке, гр. — группа щита, Н — высота оси, мм
- выключатель одноклавишный
- выключатель двухклавишный (флажков — по числу клавиш)
- привязки точек и выводов от угла и от пола, мм
- мебель и приборы — фасад по расстановке (условно)
- картина (декор): марка Д, крест — центр, Н — высота центра, мм
- дверь скрытого монтажа: полотно в плоскости стены (узел — на листе узлов)
- стены и перекрытия в сечении
- окраска: тон — цвет по коду производителя (условно)
- О1 — марка отделки по реестру отделки альбома
- А — марка развёртки: буква стены, стрелка — взгляд

Ведомость отделки (на листе)

Марка	Поверхность	Материал, изделие	Цвет, код	Кол.
О1	стены	окраска, Tikkurila Euro Power 7, колеровка по NCS, матовая, подготовка Q3	NCS S 0804-Y30R «S 0804-Y30R»	11,5 м²
О4	плинтус	плинтус МДФ, h 80 мм, аналог: плинтус МДФ под покраску 80×16	NCS S 0804-Y30R «S 0804-Y30R»	2,5 м
О5	потолок	окраска, Tikkurila Euro Power 7, глубокоматовая, подготовка Q3	Tikkurila F485 «Damask»	20,8 м²

Допущения и предложения на листе

Основа листа: размеры помещений и положение проёмов введены заказчиком в брифе, на объекте не замерены (К-1); высота потолка 2700 мм — по брифу заказчика, не замерена (К-2); толщины стен приняты по брифу: наружные 200 мм, внутренние 150 мм — не обмерены (К-1); тип дома монолитный, перекрытие 200 мм — по брифу заказчика, документов нет (К-3); планировка (стены, проёмы, объединение кухни и гостиной, расширение санузла) — по брифу без обмера и плана БТИ (К-7); разрешённая мощность 10 кВт принята, ТУ не переданы (К-8); вентканалы приняты, в брифе не заданы (К-9); подрайон климата не задан — принят не северный (жилые от 2,5 м) (К-10).

Знак «*» — принято, не замерено и не подтверждено (замерить на объекте): К-1: окно пом. 1 (стена А) — окно: положение, ширина, высота и подоконник — по брифу заказчика, не замерены; ограждение 900 мм — предложение исполнителя; дверь пом. 1 (стена В) — проём в существующей стене между пом. 1 и 5: положение и ширина — по брифу заказчика, не замерены.

Знак «**» — предложение проектировщика, заказчиком не утверждено (согласовать с заказчиком): записи в реестре нет: S11, S12 — светорегулятор добавлен разработчиком проекта.

См. лист открытых вопросов (лист 5, записи К-1–К-3, К-7–К-10).

Примечания

1. Развёртки — вид на стену изнутри помещения, по часовой стрелке; расположение — на схеме листа и на листе 62; размеры — в мм по чистовым поверхностям; отметки — в м от ±0,000; высоты Н — от чистого пола помещения до оси изделия, у декора — до центра.
2. Красные цепочки — привязки электроточек и выводов: по горизонтали от угла чистовых стен, по вертикали от чистого пола, до оси изделия; звенья короче 3 мм на листе вынесены во второй ярус (ближняя к стене цепочка).
3. У знака электроточки: марка (Р — розетка, S — выключатель, Св — светильник, ЭВ — вывод кабеля), ×N — число постов в рамке, гр. — группа щита, Н — высота оси от чистого пола, мм; группы по клавишам выключателя — на листе выключателей.
4. Схема мебели, приборов и декора не является технической документацией для производства мебели; габариты — по паспортам изделий.
5. Картины и зеркала крепить к основанию по паспорту изделия (закладные и анкеры — в перечне скрытых работ); крест — ось центра предмета.
6. Двери скрытого монтажа — полотно в плоскости стены, отделка стены по полотну, плинтус прерывается у короба (узел — на листе узлов).
7. Потолок на развёртках — по нижнему уровню У2; другие уровни потолка помещения: У1 +2,600.

1000 мм · печать 1:1

Изм.	Кол.уч	Лист	№ док.	Подп.	Дата
Разраб.		Кырлан А.С.			21.10.26
Пров.					
ГИП					
Н. контр.					
Утв.					

ГД-2026-011-АИ

Квартира 56 м²

ЖК «Северный парк», Москва

Дизайн-проект интерьера

Стадия	Лист	Листов
РП	65	83

Развёртка стены В. Гостиная-кухня (пом. 1)

М 1:25

Кырлан Александр Сергеевич


выпуск 19.10.2026 № 1c3e34763b · стр. 76 из 117

Развёртки стен А, Б. Спальня (пом. 2)


Спальня (пом. 2) · вид изнутри помещения · размеры в мм, отметки в м

ПРЕДВАРИТЕЛЬНО · не для производства работ · открыто пунктов: 10 (реестр — л. 5)

Развёртка стены А

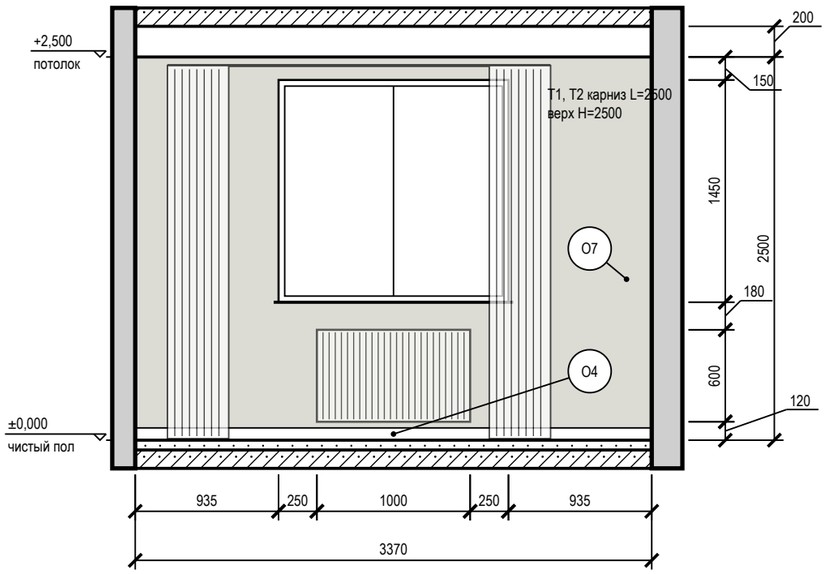


Развёртка стены Б

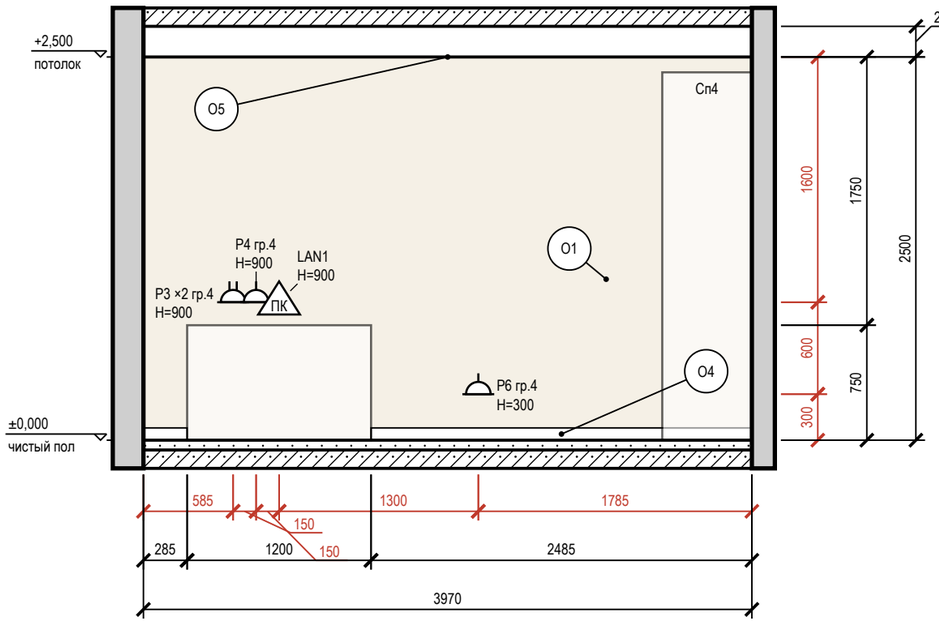

Условные обозначения

- розетка с заземляющим контактом; у знака — марка, ×N постов в рамке, гр. — группа щита, H — высота оси, мм
- ПК — розетка компьютерная RJ45
- привязки точек и выводов от угла и от пола, мм
- мебель и приборы — фасад по расстановке (условно)
- карниз (шина) и шторы в собранном виде: марка T, длина L, верх H
- окно: проём, рама, подоконник
- радиатор отопления; марка — по плану отопления
- стены и перекрытия в сечении
- окраска: тон — цвет по коду производителя (условно)
- О1 — марка отделки по реестру отделки альбома
- А — марка развёртки: буква стены, стрелка — взгляд

Схема развёрток (М 1:100)

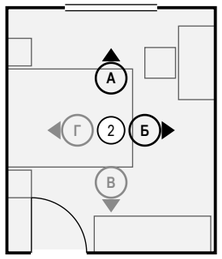

Ведомость отделки (на листе)

Марка	Поверхность	Материал, изделие	Цвет, код	Кол.
О1	стены	окраска, Tikkurila Euro Power 7, колеровка по NCS, матовая, подготовка Q3	NCS S 0804-Y30R «S 0804-Y30R»	9,9 м²
О4	плинтус	плинтус МДФ, h 80 мм, аналог: плинтус МДФ под покраску 80×16	NCS S 0804-Y30R «S 0804-Y30R»	6,1 м
О5	потолок	окраска, Tikkurila Euro Power 7, глубокоматовая, подготовка Q3	Tikkurila F485 «Damask»	13,6 м²
О7	акцентная стена	окраска, Tikkurila Euro Power 7, колеровка по NCS, матовая, подготовка Q3	NCS S 5010-G70Y «S 5010-G70Y»	6,3 м²

Допущения и предложения на листе

Основа листа: размеры помещений и положение проёмов введены заказчиком в брифе, на объекте не замерены (К-1); высота потолка 2700 мм — по брифу заказчика, не замерена (К-2); толщины стен приняты по брифу: наружные 200 мм, внутренние 150 мм — не обмерены (К-1); тип дома монолитный, перекрытие 200 мм — по брифу заказчика, документов нет (К-3); планировка (стены, проёмы, объединение кухни и гостиной, расширение санузла) — по брифу без обмера и плана БТИ (К-7); разрешённая мощность 10 кВт принята, ТУ не переданы (К-8); вентканалы приняты, в брифе не заданы (К-9); подрайон климата не задан — принят не северный (жилые от 2,5 м) (К-10).

Знак «*» — принято, не замерено и не подтверждено (замерить на объекте): К-1: окно пом. 2 (стена А) — окно: положение, ширина, высота и подоконник — по брифу заказчика, не замерены; дверь пом. 2 (стена В) — проём в существующей стене между пом. 2 и 5: положение и ширина — по брифу заказчика, не замерены.

См. лист открытых вопросов (лист 5, записи К-1–К-3, К-7–К-10).

Примечания

1. Развёртки — вид на стену изнутри помещения, по часовой стрелке; расположение — на схеме листа и на листе 62; размеры — в мм по чистовым поверхностям; отметки — в м от ±0,000; высоты H — от чистого пола помещения до оси изделия, у декора — до центра.
2. Красные цепочки — привязки электроточек и выводов: по горизонтали от угла чистовых стен, по вертикали от чистого пола, до оси изделия; звенья короче 3 мм на листе вынесены во второй ярус (ближняя к стене цепочка).
3. У знака электроточки: марка (Р — розетка, S — выключатель, Св — светильник, ЭВ — вывод кабеля), ×N — число постов в рамке, гр. — группа щита, H — высота оси от чистого пола, мм; группы по клавишам выключателя — на листе выключателей.
4. Схема мебели, приборов и декора не является технической документацией для производства мебели; габариты — по паспортам изделий.
5. Карнизы (шины) — по ведомости текстиля декоратора; длина L и верх H — по развёртке, крепление — до окраски потолка.
6. Потолок на развёртках — по нижнему уровню У1; другие уровни потолка помещения: У2 +2,600.

1000 мм · печать 1:1

Изм.	Кол.уч	Лист	№ док.	Подп.	Дата
Разраб.		Кырлан А.С.			21.10.26
Пров.					
ГИП					
Н. контр.					
Утв.					

ГД-2026-011-АИ

Квартира 56 м²

ЖК «Северный парк», Москва

Дизайн-проект интерьера

Стадия	Лист	Листов
РП	66	83

Развёртки стен А, Б. Спальня (пом. 2)

М 1:40


Кырлан Александр Сергеевич

выпуск 19.10.2026 № 1c3e34763b · стр. 77 из 117

Развёртки стен В, Г. Спальня (пом. 2)

Спальня (пом. 2) · вид изнутри помещения · размеры в мм, отметки в м

Развёртка стены В

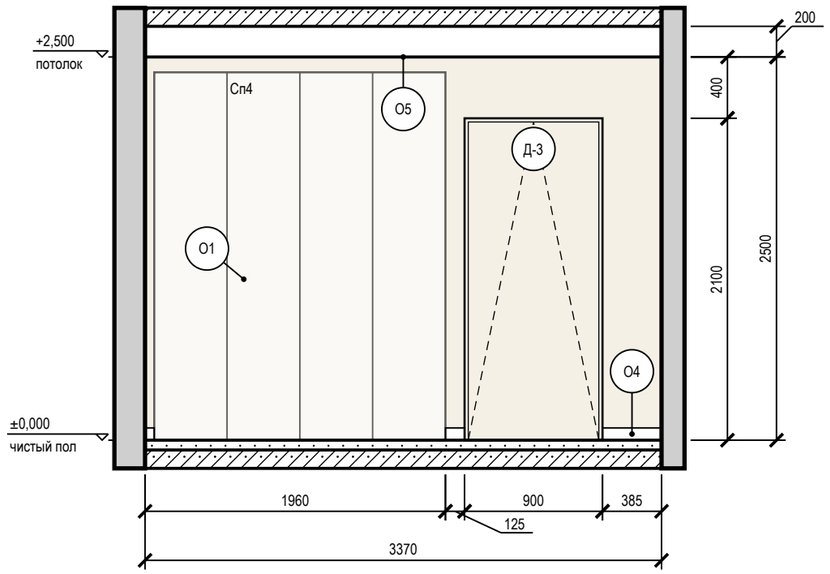

Развёртка стены Г


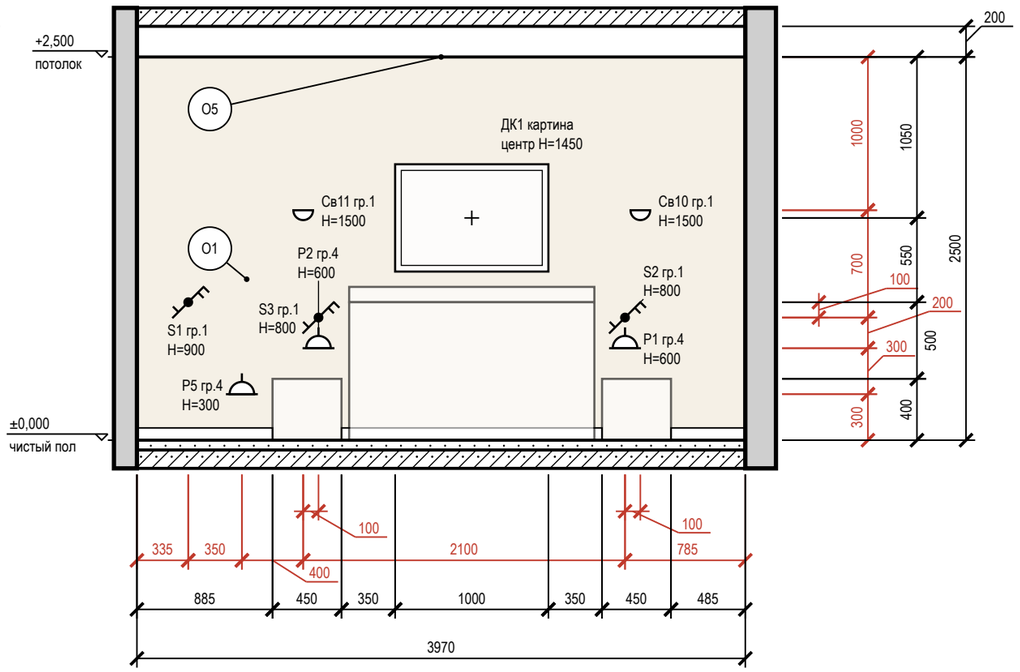


Схема развёрток (М 1:100)

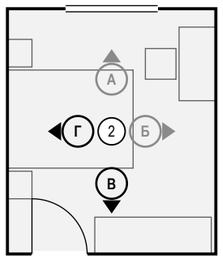

Условные обозначения

- розетка с заземляющим контактом; у знака — марка, ×N постов в рамке, гр. — группа щита, Н — высота оси, мм
- выключатель одноклавишный
- выключатель двухклавишный (флажков — по числу клавиш)
- выключатель с проходной или перекрёстной клавишей (обратный флажок); тип клавиши — в подписи
- светильник настенный (бра), Н — высота оси
- привязки точек и выводов от угла и от пола, мм
- мебель и приборы — фасад по расстановке (условно)
- картина (декор): марка Д, крест — центр, Н — высота центра, мм
- дверь скрытого монтажа: полотно в плоскости стены (узел — на листе узлов)
- стены и перекрытия в сечении
- окраска: тон — цвет по коду производителя (условно)
- О1 — марка отделки по реестру отделки альбома
- А — марка развёртки: буква стены, стрелка — взгляд

Ведомость отделки (на листе)

Марка	Поверхность	Материал, изделие	Цвет, код	Кол.
О1	стены	окраска, Tikkurila Euro Power 7, колеровка по NCS, матовая, подготовка Q3	NCS S 0804-Y30R «S 0804-Y30R»	16,5 м²
О4	плинтус	плинтус МДФ, h 80 мм, аналог: плинтус МДФ под покраску 80×16	NCS S 0804-Y30R «S 0804-Y30R»	3,6 м
О5	потолок	окраска, Tikkurila Euro Power 7, глубокоматовая, подготовка Q3	Tikkurila F485 «Damask»	13,6 м²

Допущения и предложения на листе

Основа листа: размеры помещений и положение проёмов введены заказчиком в брифе, на объекте не замерены (К-1); высота потолка 2700 мм — по брифу заказчика, не замерена (К-2); толщины стен приняты по брифу: наружные 200 мм, внутренние 150 мм — не обмерены (К-1); тип дома монолитный, перекрытие 200 мм — по брифу заказчика, документов нет (К-3); планировка (стены, проёмы, объединение кухни и гостиной, расширение санузла) — по брифу без обмера и плана БТИ (К-7); разрешённая мощность 10 кВт принята, ТУ не переданы (К-8); вентканалы приняты, в брифе не заданы (К-9); подрайон климата не задан — принят не северный (жилые от 2,5 м) (К-10).

Знак «*» — принято, не замерено и не подтверждено (замерить на объекте): К-1: окно пом. 2 (стена А) — окно: положение, ширина, высота и подоконник — по брифу заказчика, не замерены; дверь пом. 2 (стена В) — проём в существующей стене между пом. 2 и 5: положение и ширина — по брифу заказчика, не замерены.

См. лист открытых вопросов (лист 5, записи К-1–К-3, К-7–К-10).

Примечания

1. Развёртки — вид на стену изнутри помещения, по часовой стрелке; расположение — на схеме листа и на листе 62; размеры — в мм по чистовым поверхностям; отметки — в м от ±0,000; высоты Н — от чистого пола помещения до оси изделия, у декора — до центра.
2. Красные цепочки — привязки электроточек и выводов: по горизонтали от угла чистовых стен, по вертикали от чистого пола, до оси изделия; звенья короче 3 мм на листе вынесены во второй ярус (ближняя к стене цепочка).
3. У знака электроточки: марка (Р — розетка, S — выключатель, Св — светильник, ЭВ — вывод кабеля), ×N — число постов в рамке, гр. — группа щита, Н — высота оси от чистого пола, мм; группы по клавишам выключателя — на листе выключателей.
4. Схема мебели, приборов и декора не является технической документацией для производства мебели; габариты — по паспортам изделий.
5. Картины и зеркала крепить к основанию по паспорту изделия (закладные и анкеры — в перечне скрытых работ); крест — ось центра предмета.
6. Двери скрытого монтажа — полотно в плоскости стены, отделка стены по полотну, плинтус прерывается у короба (узел — на листе узлов).
7. Потолок на развёртках — по нижнему уровню У1; другие уровни потолка помещения: У2 +2,600.

1000 мм · печать 1:1

Изм.	Кол.уч	Лист	№ док.	Подп.	Дата
Разраб.		Кырлан А.С.			21.10.26
Пров.					
ГИП					
Н. контр.					
Утв.					

ГД-2026-011-АИ

Квартира 56 м²

ЖК «Северный парк», Москва

Дизайн-проект интерьера

Стадия	Лист	Листов
РП	67	83

Развёртки стен В, Г. Спальня (пом. 2)

М 1:40

Кырлан Александр Сергеевич


выпуск 19.10.2026 № 1c3e34763b · стр. 78 из 117

Развёртки стен А, Б. Детская (пом. 3)

Детская (пом. 3) · вид изнутри помещения · размеры в мм, отметки в м

ПРЕДВАРИТЕЛЬНО · не для производства работ · открыто пунктов: 10 (реестр — л. 5)

Развёртка стены А

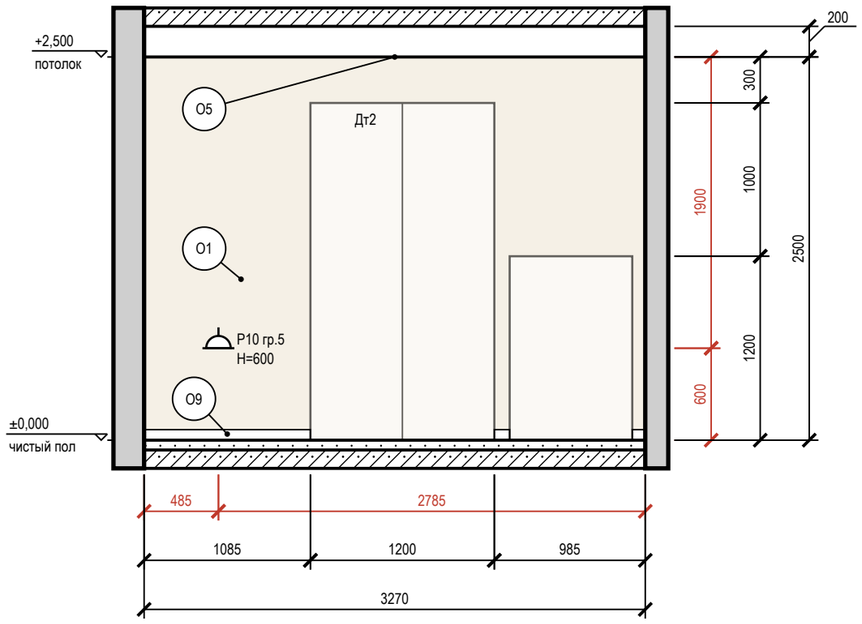

Развёртка стены Б


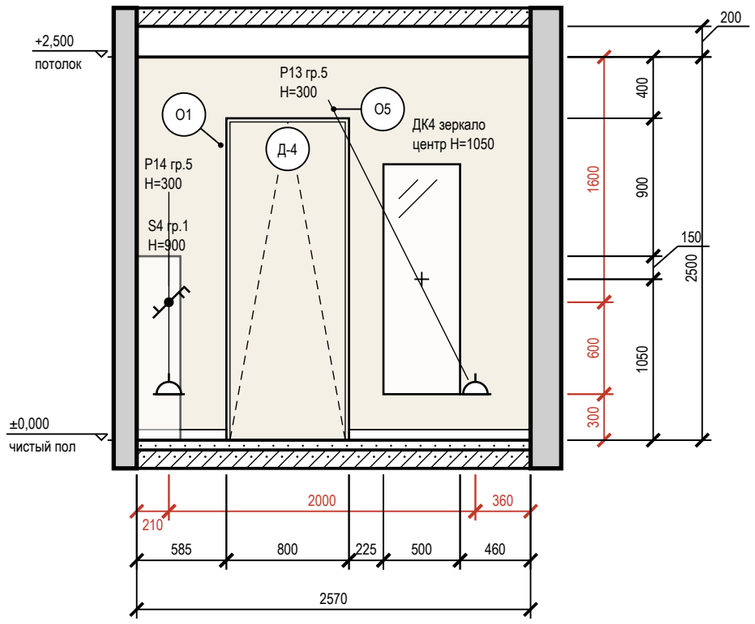


Схема развёрток (М 1:100)

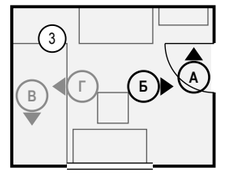

Условные обозначения

- розетка с заземляющим контактом; у знака — марка, ×N постов в рамке, гр. — группа щита, Н — высота оси, мм
- выключатель одноклавишный
- выключатель двухклавишный (флажков — по числу клавиш)
- выключатель с проходной или перекрёстной клавишей (обратный флажок); тип клавиши — в подписи
- привязки точек и выводов от угла и от пола, мм
- мебель и приборы — фасад по расстановке (условно)
- зеркало: марка Д, крест — центр, Н — высота центра, мм
- дверь скрытого монтажа: полотно в плоскости стены (узел — на листе узлов)
- стены и перекрытия в сечении
- окраска: тон — цвет по коду производителя (условно)
- О1 — марка отделки по реестру отделки альбома
- А — марка развёртки: буква стены, стрелка — взгляд

Ведомость отделки (на листе)

Марка	Поверхность	Материал, изделие	Цвет, код	Кол.
О1	стены	окраска, Tikkurila Euro Power 7, колеровка по NCS, матовая, подготовка Q3	NCS S 0804-Y30R «S 0804-Y30R»	12,9 м²
О5	потолок	окраска, Tikkurila Euro Power 7, глубокоматовая, подготовка Q3	Tikkurila F485 «Damask»	8,6 м²
О9	плинтус	плинтус МДФ, Orac Decor Contour (Luxxus), h 69 мм, SX165	NCS S 0804-Y30R «S 0804-Y30R»	3 м

Допущения и предложения на листе

Основа листа: размеры помещений и положение проёмов введены заказчиком в брифе, на объекте не замерены (К-1); высота потолка 2700 мм — по брифу заказчика, не замерена (К-2); толщины стен приняты по брифу: наружные 200 мм, внутренние 150 мм — не обмерены (К-1); тип дома монолитный, перекрытие 200 мм — по брифу заказчика, документов нет (К-3); планировка (стены, проёмы, объединение кухни и гостиной, расширение санузла) — по брифу без обмера и плана БТИ (К-7); разрешённая мощность 10 кВт принята, ТУ не переданы (К-8); вентканалы приняты, в брифе не заданы (К-9); подрайон климата не задан — принят не северный (жилые от 2,5 м) (К-10).

Знак «*» — принято, не замерено и не подтверждено (замерить на объекте): К-1: окно пом. 3 (стена В) — окно: положение, ширина, высота и подоконник — по брифу заказчика, не замерены.

Знак «**» — предложение проектировщика, заказчиком не утверждено (согласовать с заказчиком): К-5: дверь пом. 3 (стена Б) — дверь в новой перегородке: проём по брифу, короб скрытой двери и размер в свету — после выбора модели и утверждения перегородки (К-5).

См. лист открытых вопросов (лист 5, записи К-1–К-3, К-5, К-7–К-10).

Примечания

1. Развёртки — вид на стену изнутри помещения, по часовой стрелке; расположение — на схеме листа и на листе 62; размеры — в мм по чистовым поверхностям; отметки — в м от ±0,000; высоты Н — от чистого пола помещения до оси изделия, у декора — до центра.
2. Красные цепочки — привязки электроточек и выводов: по горизонтали от угла чистовых стен, по вертикали от чистого пола, до оси изделия; звенья короче 3 мм на листе вынесены во второй ярус (ближняя к стене цепочка).
3. У знака электроточки: марка (Р — розетка, S — выключатель, Св — светильник, ЭВ — вывод кабеля), ×N — число постов в рамке, гр. — группа щита, Н — высота оси от чистого пола, мм; группы по клавишам выключателя — на листе выключателей.
4. Схема мебели, приборов и декора не является технической документацией для производства мебели; габариты — по паспортам изделий.
5. Картины и зеркала крепить к основанию по паспорту изделия (закладные и анкеры — в перечне скрытых работ); крест — ось центра предмета.
6. Двери скрытого монтажа — полотно в плоскости стены, отделка стены по полотну, плинтус прерывается у короба (узел — на листе узлов).
7. Потолок на развёртках — по нижнему уровню У1; другие уровни потолка помещения: У2 +2,600.

1000 мм · печать 1:1

Изм.	Кол.уч	Лист	№ док.	Подп.	Дата
Разраб.		Кырлан А.С.			21.10.26
Пров.					
ГИП					
Н. контр.					
Утв.					

ГД-2026-011-АИ

Квартира 56 м²

ЖК «Северный парк», Москва

Дизайн-проект интерьера

Стадия	Лист	Листов
РП	68	83

Развёртки стен А, Б. Детская (пом. 3)

М 1:40

Кырлан Александр Сергеевич


выпуск 19.10.2026 № 1c3e34763b · стр. 79 из 117

Развёртки стен В, Г. Детская (пом. 3)


Детская (пом. 3) · вид изнутри помещения · размеры в мм, отметки в м

ПРЕДВАРИТЕЛЬНО · не для производства работ · открыто пунктов: 10 (реестр — л. 5)

Развёртка стены В

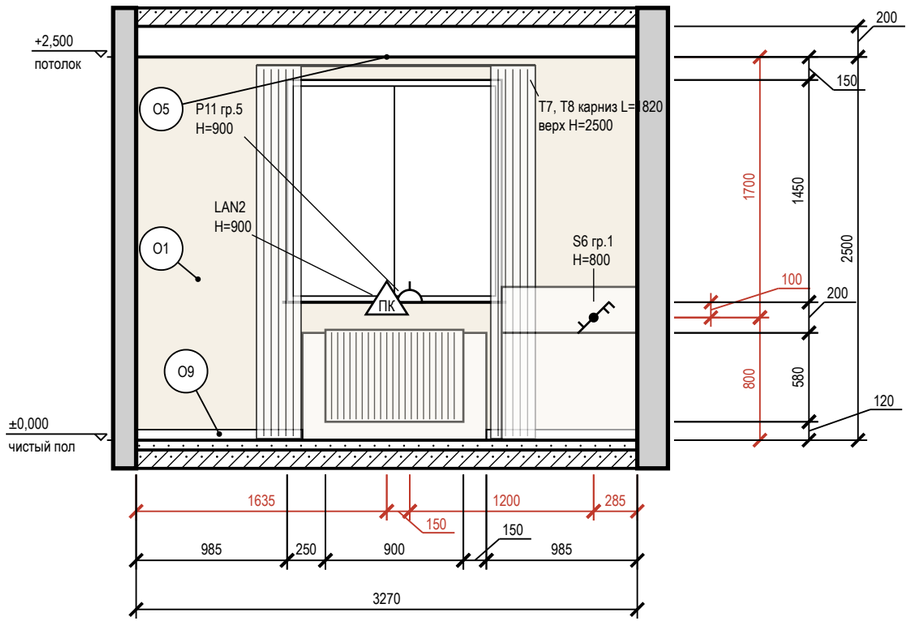


Развёртка стены Г

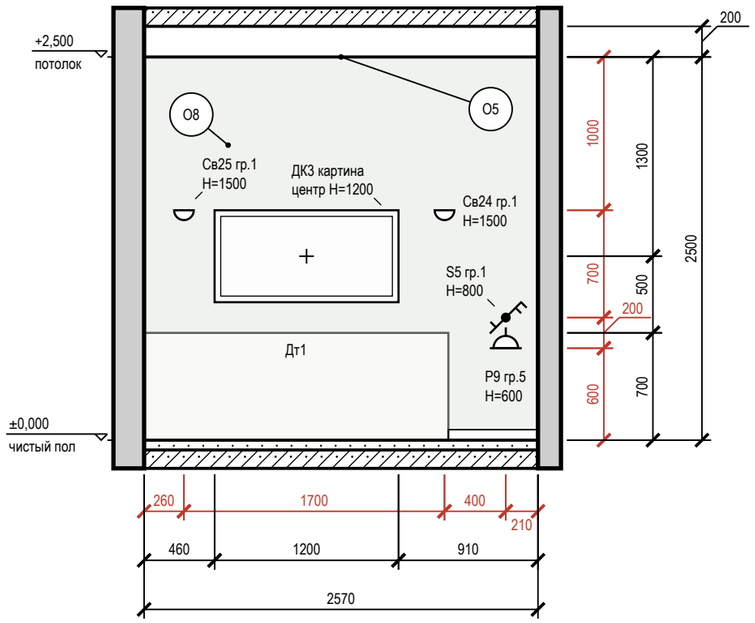

Условные обозначения

- розетка с заземляющим контактом; у знака — марка, ×N постов в рамке, гр. — группа щита, Н — высота оси, мм
- выключатель одноклавишный
- выключатель двухклавишный (флажков — по числу клавиш)
- выключатель с проходной или перекрёстной клавишей (обратный флажок); тип клавиши — в подписи
- светильник настенный (бра), Н — высота оси
- ПК — розетка компьютерная RJ45
- привязки точек и выводов от угла и от пола, мм
- мебель и приборы — фасад по расстановке (условно)
- картина (декор): марка Д, крест — центр, Н — высота центра, мм
- карниз (шина) и шторы в собранном виде: марка Т, длина L, верх Н
- окно: проём, рама, подоконник
- радиатор отопления; марка — по плану отопления
- стены и перекрытия в сечении
- окраска: тон — цвет по коду производителя (условно)
- О1 — марка отделки по реестру отделки альбома
- А — марка развёртки: буква стены, стрелка — взгляд

Схема развёрток (М 1:100)

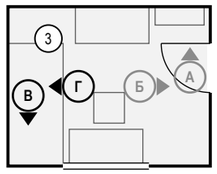

Ведомость отделки (на листе)

Марка	Поверхность	Материал, изделие	Цвет, код	Кол.
О1	стены	окраска, Tikkurila Euro Power 7, колеровка по NCS, матовая, подготовка Q3	NCS S 0804-Y30R «S 0804-Y30R»	6,1 м²
О5	потолок	окраска, Tikkurila Euro Power 7, глубокоматовая, подготовка Q3	Tikkurila F485 «Damask»	8,6 м²
О8	акцентная стена	окраска, Tikkurila Euro Power 7, матовая, подготовка Q3	Tikkurila X447 «Sea Smoke»	6,4 м²
О9	плинтус	плинтус МДФ, Orac Decor Contour (Luxxus), h 69 мм, SX165	NCS S 0804-Y30R «S 0804-Y30R»	2,7 м

Допущения и предложения на листе

Основа листа: размеры помещений и положение проёмов введены заказчиком в брифе, на объекте не замерены (К-1); высота потолка 2700 мм — по брифу заказчика, не замерена (К-2); толщины стен приняты по брифу: наружные 200 мм, внутренние 150 мм — не обмерены (К-1); тип дома монолитный, перекрытие 200 мм — по брифу заказчика, документов нет (К-3); планировка (стены, проёмы, объединение кухни и гостиной, расширение санузла) — по брифу без обмера и плана БТИ (К-7); разрешённая мощность 10 кВт принята, ТУ не переданы (К-8); вентканалы приняты, в брифе не заданы (К-9); подрайон климата не задан — принят не северный (жилые от 2,5 м) (К-10).

Знак «*» — принято, не замерено и не подтверждено (замерить на объекте): К-1: окно пом. 3 (стена В) — окно: положение, ширина, высота и подоконник — по брифу заказчика, не замерены.

Знак «**» — предложение проектировщика, заказчиком не утверждено (согласовать с заказчиком): К-5: дверь пом. 3 (стена Б) — дверь в новой перегородке: проём по брифу, короб скрытой двери и размер в свету — после выбора модели и утверждения перегородки (К-5).

См. лист открытых вопросов (лист 5, записи К-1–К-3, К-5, К-7–К-10).

Примечания

1. Развёртки — вид на стену изнутри помещения, по часовой стрелке; расположение — на схеме листа и на листе 62; размеры — в мм по чистовым поверхностям; отметки — в м от ±0,000; высоты Н — от чистого пола помещения до оси изделия, у декора — до центра.
2. Красные цепочки — привязки электроточек и выводов: по горизонтали от угла чистовых стен, по вертикали от чистого пола, до оси изделия; звенья короче 3 мм на листе вынесены во второй ярус (ближняя к стене цепочка).
3. У знака электроточки: марка (Р — розетка, S — выключатель, Св — светильник, ЭВ — вывод кабеля), ×N — число постов в рамке, гр. — группа щита, Н — высота оси от чистого пола, мм; группы по клавишам выключателя — на листе выключателей.
4. Схема мебели, приборов и декора не является технической документацией для производства мебели; габариты — по паспортам изделий.
5. Картины и зеркала крепить к основанию по паспорту изделия (закладные и анкеры — в перечне скрытых работ); крест — ось центра предмета.
6. Карнизы (шины) — по ведомости текстиля декоратора; длина L и верх Н — по развёртке, крепление — до окраски потолка.
7. Потолок на развёртках — по нижнему уровню У1; другие уровни потолка помещения: У2 +2,600.

1000 мм · печать 1:1

Изм.	Кол.уч	Лист	№ док.	Подп.	Дата
Разраб.		Кырлан А.С.			21.10.26
Пров.					
ГИП					
Н. контр.					
Утв.					

ГД-2026-011-АИ

Квартира 56 м²

ЖК «Северный парк», Москва

Дизайн-проект интерьера

Стадия	Лист	Листов
РП	69	83

Развёртки стен В, Г. Детская (пом. 3)

М 1:40

Кырлан Александр Сергеевич


выпуск 19.10.2026 № 1c3e34763b · стр. 80 из 117

Развёртка стены А. Санузел (пом. 4)

Санузел (пом. 4) · вид изнутри помещения · размеры в мм, отметки в м

ПРЕДВАРИТЕЛЬНО · не для производства работ · открыто пунктов: 10 (реестр — л. 5)

Развёртка стены А

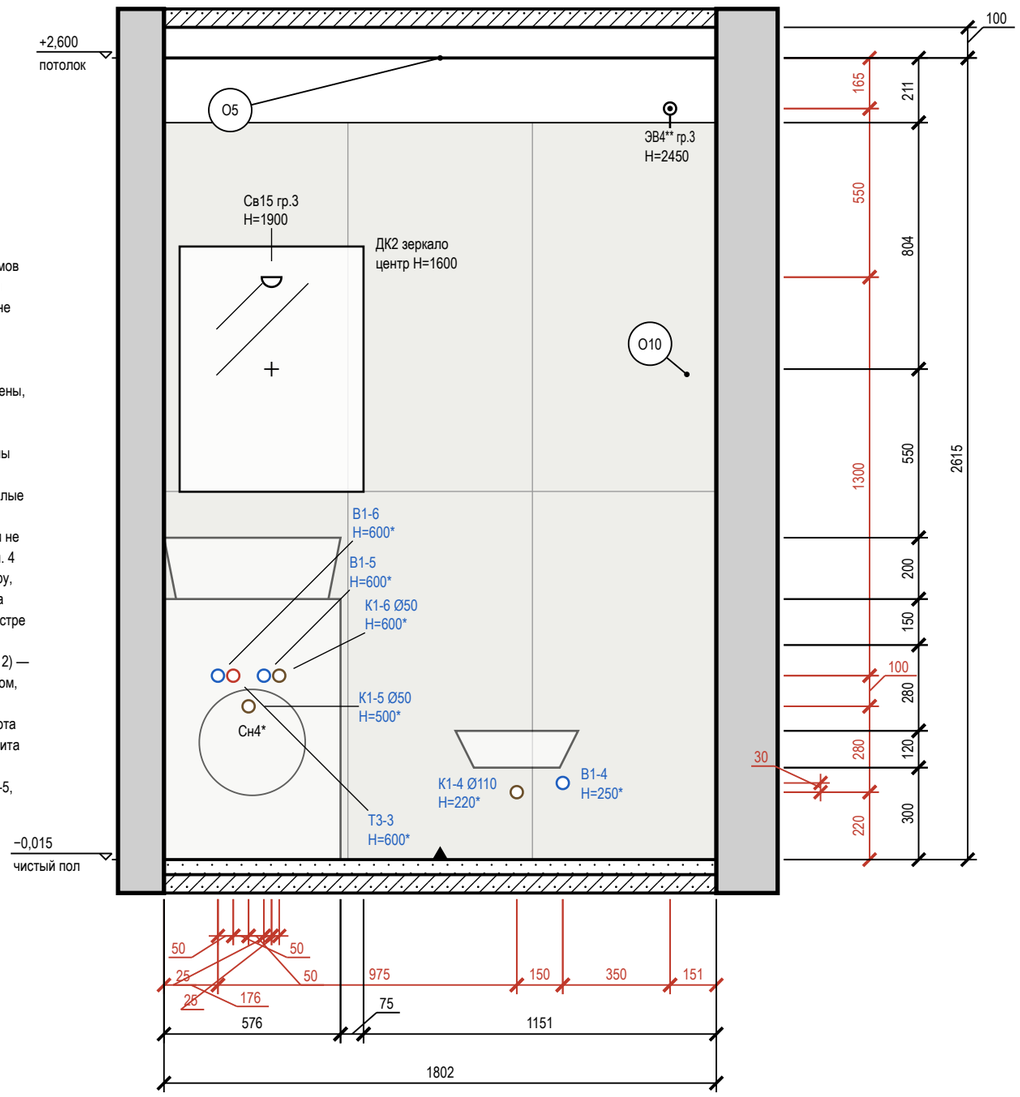


Допущения и предложения на листе

Основа листа: размеры помещений и положение проёмов введены заказчиком в брифе, на объекте не замерены (К-1); высота потолка 2700 мм — по брифу заказчика, не замерена (К-2); толщины стен приняты по брифу: наружные 200 мм, внутренние 150 мм — не обмерены (К-1); тип дома монолитный, перекрытие 200 мм — по брифу заказчика, документов нет (К-3); планировка (стены, проёмы, объединение кухни и гостиной, расширение санузла) — по брифу без обмера и плана БТИ (К-7); разрешённая мощность 10 кВт принята, ТУ не переданы (К-8); вентканалы приняты, в брифе не заданы (К-9); подрайон климата не задан — принят не северный (жилые от 2,5 м) (К-10).

Знак «**» — предложение проектировщика, заказчиком не утверждено (согласовать с заказчиком): К-5: дверь пом. 4 (стена Г) — дверь в новой перегородке: проём по брифу, короб скрытой двери и размер в свету — после выбора модели и утверждения перегородки (К-5); записи в реестре нет: ЭВ4 — по образцу: Добавлены выводы к вентиляторам: ЭВ4 (ВР1, ванная) и ЭВ5 (ВР3, санузел 2) — группа 3, высота 2389 мм, включение с основным светом, таймер выбега в вентиляторе; и коробки уравнивания потенциалов КУП1 (ванная) и КУП2 (санузел 2) — высота 300 мм, у входа, вне зон 0–2, проводник от шины РЕ щита ЩК, сече.

См. лист открытых вопросов (лист 5, записи К-1–К-3, К-5, К-7–К-10).

Схема развёрток (М 1:100)

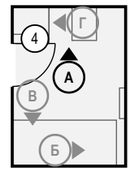

Условные обозначения

- вывод кабеля для подключения прибора (без розетки), марка ЭВ
- светильник настенный (бра), Н — высота оси
- вывод В1 (код — в ведомости привязок)
- вывод Т3 (код — в ведомости привязок)
- вывод К1 (код — в ведомости привязок)
- привязки точек и выводов от угла и от пола, мм
- мебель и приборы — фасад по расстановке (условно)
- зеркало: марка Д, крест — центр, Н — высота центра, мм
- стены и перекрытия в сечении
- плитка: сетка швов по формату, ▲ — ось старта
- О1 — марка отделки по реестру отделки альбома
- А — марка развёртки: буква стены, стрелка — взгляд

Ведомость отделки (на листе)

Марка	Поверхность	Материал, изделие	Цвет, код	Кол.
О5	потолок	окраска, Tikkurila Euro Power 7, матовая, подготовка Q3	Tikkurila F485 «Damask»	4,8 м²
О10	стены	облицовка плиткой, Atlas Concorde Marvel Travertine, 600×1200×9 мм, А8UZ, затирка CG2WA	Atlas Concorde A8UZ «Marvel Travertine»	4,3 м²

Примечания

1. Развёртки — вид на стену изнутри помещения, по часовой стрелке; расположение — на схеме листа и на листе 62; размеры — в мм по чистовым поверхностям; отметки — в м от ±0,000; высоты Н — от чистого пола помещения до оси изделия, у декора — до центра.
2. Красные цепочки — привязки электроточек и выводов: по горизонтали от угла чистовых стен, по вертикали от чистого пола, до оси изделия; звенья короче 3 мм на листе вынесены во второй ярус (ближняя к стене цепочка).
3. У знака электроточки: марка (Р — розетка, S — выключатель, Св — светильник, ЭВ — вывод кабеля), ×N — число постов в рамке, гр. — группа щита, Н — высота оси от чистого пола, мм; группы по клавишам выключателя — на листе выключателей.
4. Схема мебели, приборов и декора не является технической документацией для производства мебели; габариты — по паспортам изделий (* — высота не задана в проекте, показана по типовому изделию).
5. Выводы ВК — коды и высоты по листу выводов сантехники; * — высота принята по типовой практике монтажа, окончательно — по паспорту прибора.
6. Облицовка — по сетке швов 2 мм, раскладка от оси стены (треугольник у пола), целые ряды от пола; подрезки — по листу раскладки плитки.
7. Гидроизоляция в 2 слоя, заход на стены 200 мм — до облицовки, с актом скрытых работ и тестом проливом (узел — на листе узлов).
8. Картины и зеркала крепить к основанию по паспорту изделия (закладные и анкеры — в перечне скрытых работ); крест — ось центра предмета.

1000 мм · печать 1:1

Изм.	Кол.уч	Лист	№ док.	Подп.	Дата
Разраб.		Кырлан А.С.			21.10.26
Пров.					
ГИП					
Н. контр.					
Утв.					

ГД-2026-011-АИ

Квартира 56 м²

ЖК «Северный парк», Москва

Дизайн-проект интерьера

Стадия	Лист	Листов
РП	70	83

Развёртка стены А. Санузел (пом. 4)

М 1:20

Кырлан Александр Сергеевич


выпуск 19.10.2026 № 1c3e34763b · стр. 81 из 117

Развёртки стен Б, В. Санузел (пом. 4)

Санузел (пом. 4) · вид изнутри помещения · размеры в мм, отметки в м

ПРЕДВАРИТЕЛЬНО · не для производства работ · открыто пунктов: 10 (реестр — л. 5)

Развёртка стены Б

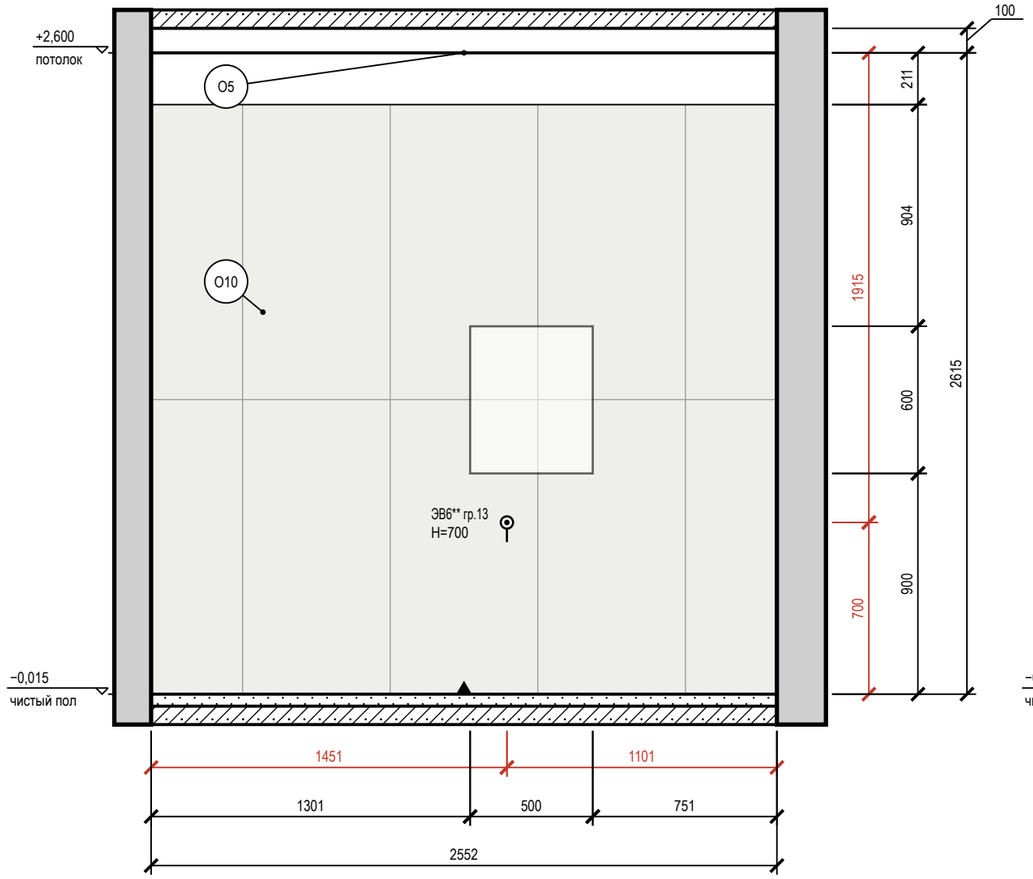

Развёртка стены В


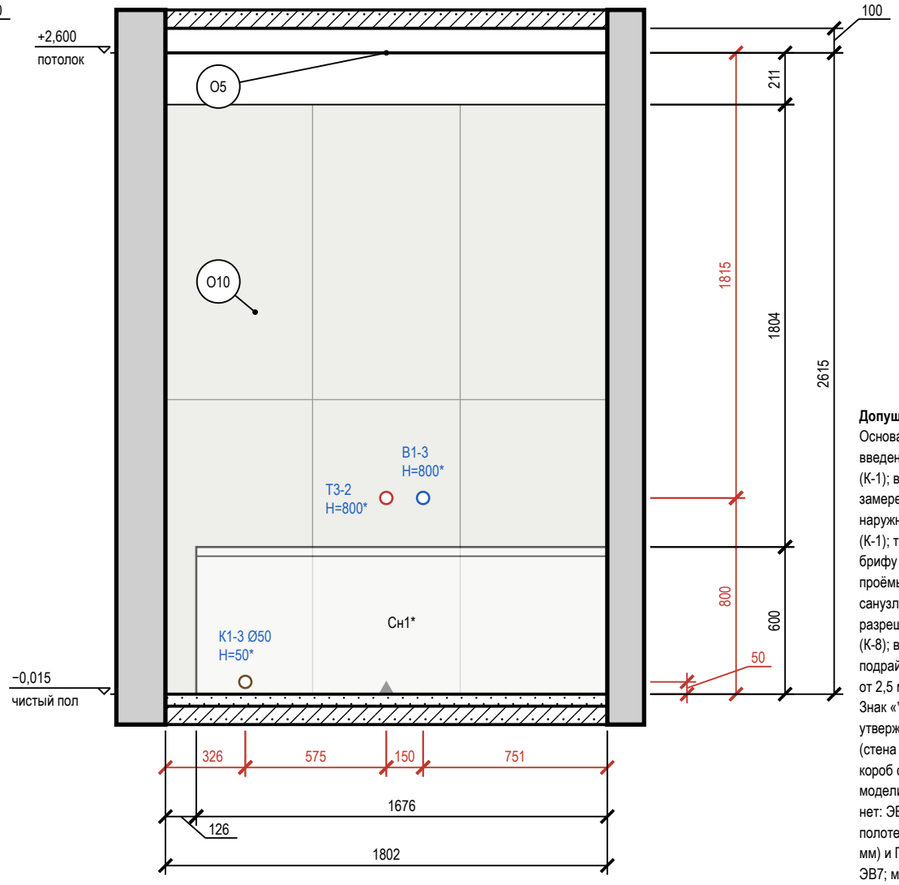


Схема развёрток (М 1:100)

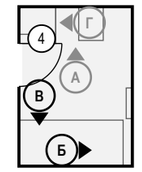

Допущения и предложения на листе

Основа листа: размеры помещений и положение проёмов введены заказчиком в брифе, на объекте не замерены (К-1); высота потолка 2700 мм — по брифу заказчика, не замерена (К-2); толщины стен приняты по брифу: наружные 200 мм, внутренние 150 мм — не обмерены (К-1); тип дома монолитный, перекрытие 200 мм — по брифу заказчика, документов нет (К-3); планировка (стены, проёмы, объединение кухни и гостиной, расширение санузла) — по брифу без обмера и плана БТИ (К-7); разрешённая мощность 10 кВт принята, ТУ не переданы (К-8); вентканалы приняты, в брифе не заданы (К-9); подрайон климата не задан — принят не северный (жилые от 2,5 м) (К-10).

Знак «**» — предложение проектировщика, заказчиком не утверждено (согласовать с заказчиком): К-5: дверь пом. 4 (стена Г) — дверь в новой перегородке: проём по брифу, короб скрытой двери и размер в свету — после выбора модели и утверждения перегородки (К-5); записи в реестре нет: ЭВ6 — по образцу: Добавлены электрические полотенцесушители IP44: П10 в ванной (480 мм, низ 900 мм) и П13 в санузле 2 (400 мм, низ 900 мм), выводы ЭВ6 и ЭВ7; мощность группы 13 — 2,4 кВт вместо 1,8 кВт.

См. лист открытых вопросов (лист 5, записи К-1–К-3, К-5, К-7–К-10).

Условные обозначения

- вывод кабеля для подключения прибора (без розетки), марка ЭВ
- вывод В1 (код — в ведомости привязок)
- вывод Т3 (код — в ведомости привязок)
- вывод К1 (код — в ведомости привязок)
- привязки точек и выводов от угла и от пола, мм
- мебель и приборы — фасад по расстановке (условно)
- стены и перекрытия в сечении
- плитка: сетка швов по формату, ▲ — ось старта
- О1 — марка отделки по реестру отделки альбома
- А — марка развёртки: буква стены, стрелка — взгляд

Ведомость отделки (на листе)

Марка	Поверхность	Материал, изделие	Цвет, код	Кол.
О5	потолок	окраска, Tikkurila Euro Power 7, матовая, подготовка Q3	Tikkurila F485 «Damask»	4,8 м²
О10	стены	облицовка плиткой, Atlas Concorde Marvel Travertine, 600×1200×9 мм, A8UZ, затирка CG2WA	Atlas Concorde A8UZ «Marvel Travertine»	10,5 м²

Примечания

1. Развёртки — вид на стену изнутри помещения, по часовой стрелке; расположение — на схеме листа и на листе 62; размеры — в мм по чистовым поверхностям; отметки — в м от ±0,000; высоты Н — от чистого пола помещения до оси изделия, у декора — до центра.
2. Красные цепочки — привязки электроточек и выводов: по горизонтали от угла чистовых стен, по вертикали от чистого пола, до оси изделия; звенья короче 3 мм на листе вынесены во второй ярус (ближняя к стене цепочка).
3. У знака электроточки: марка (Р — розетка, S — выключатель, Св — светильник, ЭВ — вывод кабеля), ×N — число постов в рамке, гр. — группа щита, Н — высота оси от чистого пола, мм; группы по клавишам выключателя — на листе выключателей.
4. Схема мебели, приборов и декора не является технической документацией для производства мебели; габариты — по паспортам изделий (* — высота не задана в проекте, показана по типовому изделию).
5. Выводы ВК — коды и высоты по листу выводов сантехники; * — высота принята по типовой практике монтажа, окончательно — по паспорту прибора.
6. Облицовка — по сетке швов 2 мм, раскладка от оси стены (треугольник у пола), целые ряды от пола; подрезки — по листу раскладки плитки.
7. Гидроизоляция в 2 слоя, заход на стены 200 мм — до облицовки, с актом скрытых работ и тестом проливом (узел — на листе узлов).

1000 мм · печать 1:1

Изм.	Кол.уч	Лист	№ док.	Подп.	Дата
Разраб.		Кырлан А.С.			21.10.26
Пров.					
ГИП					
Н. контр.					
Утв.					

ГД-2026-011-АИ

Квартира 56 м²

ЖК «Северный парк», Москва

Дизайн-проект интерьера

Стадия	Лист	Листов
РП	71	83

Развёртки стен Б, В. Санузел (пом. 4)

М 1:25

Кырлан Александр Сергеевич

выпуск 19.10.2026 № 1c3e34763b · стр. 82 из 117

Развёртка стены Г. Санузел (пом. 4)

Санузел (пом. 4) · вид изнутри помещения · размеры в мм, отметки в м

Развёртка стены Г


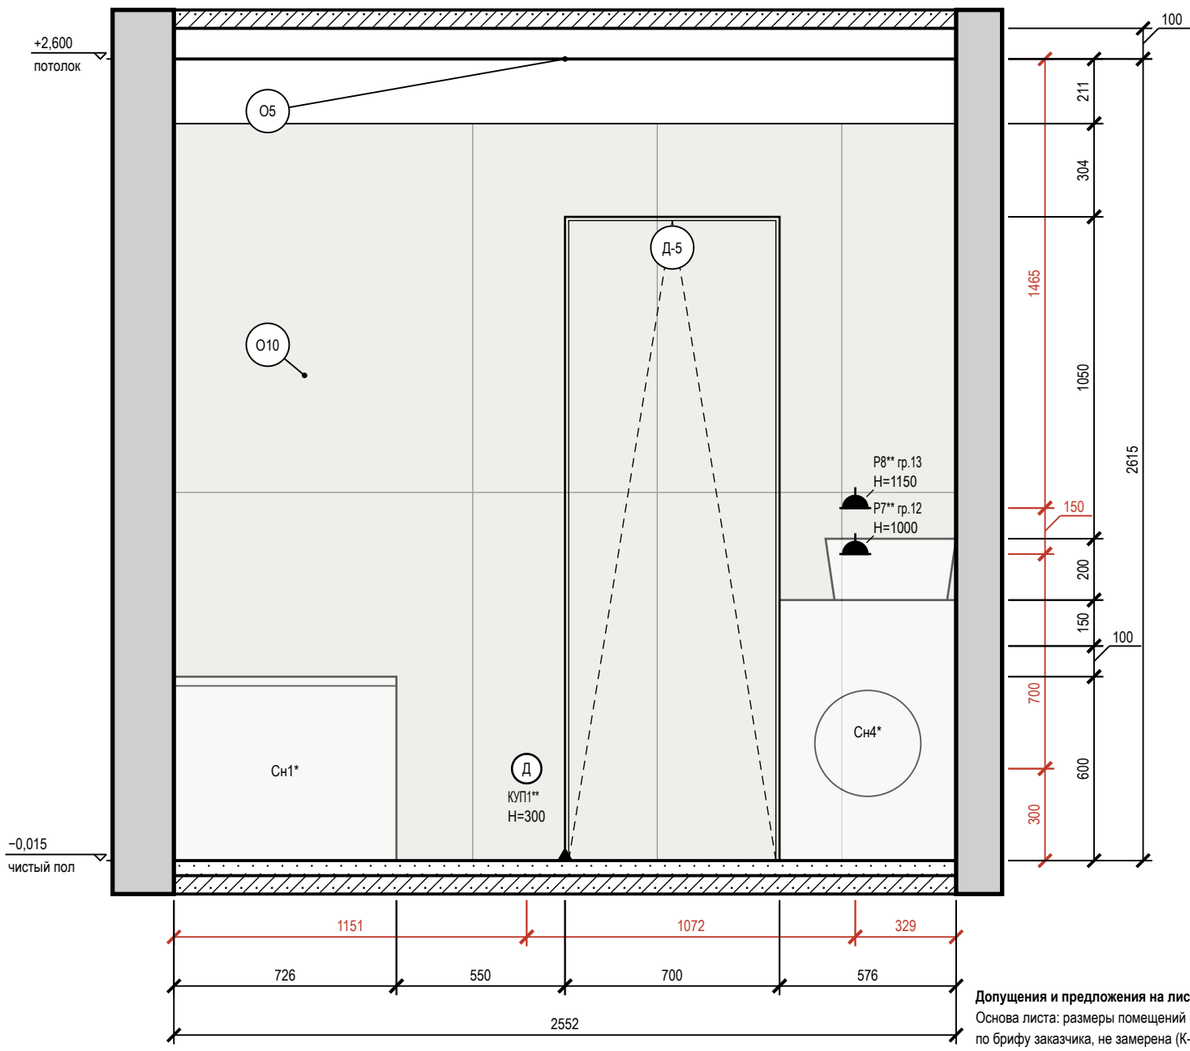


Схема развёрток (М 1:100)

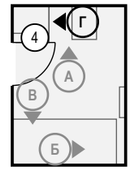

Условные обозначения

- розетка влагозащищённая IP44
- привязки точек и выводов от угла и от пола, мм
- мебель и приборы — фасад по расстановке (условно)
- дверь скрытого монтажа: полотно в плоскости стены (узел — на листе узлов)
- стены и перекрытия в сечении
- плитка: сетка швов по формату, ▲ — ось старта
- О1 — марка отделки по реестру отделки альбома
- А — марка развёртки: буква стены, стрелка — взгляд

Ведомость отделки (на листе)

Марка	Поверхность	Материал, изделие	Цвет, код	Кол.
О5	потолок	окраска, Tikkurila Euro Power 7, матовая, подготовка Q3	Tikkurila F485 «Damask»	4,8 м²
О10	стены	облицовка плиткой, Atlas Concorde Marvel Travertine, 600×1200×9 мм, A8UZ, затирка CG2WA	Atlas Concorde A8UZ «Marvel Travertine»	4,7 м²

Допущения и предложения на листе

Основа листа: размеры помещений и положение проёмов введены заказчиком в брифе, на объекте не замерены (К-1); высота потолка 2700 мм — по брифу заказчика, не замерена (К-2); толщины стен приняты по брифу: наружные 200 мм, внутренние 150 мм — не обмерены (К-1); тип дома монолитный, перекрытие 200 мм — по брифу заказчика, документов нет (К-3); планировка (стены, проёмы, объединение кухни и гостиной, расширение санузла) — по брифу без обмера и плана БТИ (К-7); разрешённая мощность 10 кВт принята, ТУ не переданы (К-8); вентканалы приняты, в брифе не заданы (К-9); подрайон климата не задан — принят не северный (жилые от 2,5 м) (К-10).
Знак «**» — предложение проектировщика, заказчиком не утверждено (согласовать с заказчиком): К-5: дверь пом. 4 (стена Г) — дверь в новой перегородке: проём по брифу, короб скрытой двери и размер в свету — после выбора модели и утверждения перегородки (К-5); записи в реестре нет: Р7, Р8 — по образцу: Р7, Р8 и Р33 на высоте 1000 мм — верхний предел нормы (ПУЭ, п. 6.6.30, не выше 1 м); флаг решения снят; КУП1 — по образцу: Добавлены выводы к вентиляторам: ЭВ4 (ВР1, ванная) и ЭВ5 (ВР3, санузел 2) — группа 3, высота 2389 мм, включение с основным светом, таймер выбега в вентиляторе; и коробки уравнивания потенциалов КУП1 (ванная) и КУП2 (санузел 2) — высота 300 мм, у входа, вне зон 0–2, проводник от шины PE щита ЩК, сече.
См. лист открытых вопросов (лист 5, записи К-1–К-3, К-5, К-7–К-10).

Примечания

1. Развёртки — вид на стену изнутри помещения, по часовой стрелке; расположение — на схеме листа и на листе 62; размеры — в мм по чистовым поверхностям; отметки — в м от ±0,000; высоты Н — от чистого пола помещения до оси изделия, у декора — до центра.
2. Красные цепочки — привязки электроточек и выводов: по горизонтали от угла чистовых стен, по вертикали от чистого пола, до оси изделия; звенья короче 3 мм на листе вынесены во второй ярус (ближняя к стене цепочка).
3. У знака электроточки: марка (Р — розетка, S — выключатель, Св — светильник, ЭВ — вывод кабеля), ×N — число постов в рамке, гр. — группа щита, Н — высота оси от чистого пола, мм; группы по клавишам выключателя — на листе выключателей.
4. Схема мебели, приборов и декора не является технической документацией для производства мебели; габариты — по паспортам изделий (* — высота не задана в проекте, показана по типовому изделию).
5. Облицовка — по сетке швов 2 мм, раскладка от оси стены (треугольник у пола), целые ряды от пола; подрезки — по листу раскладки плитки.
6. Гидроизоляция в 2 слоя, заход на стены 200 мм — до облицовки, с актом скрытых работ и тестом проливом (узел — на листе узлов).
7. Двери скрытого монтажа — полотно в плоскости стены, отделка стены по полотну, плинтус прерывается у короба (узел — на листе узлов).

1000 мм · печать 1:1

Изм.	Кол.уч	Лист	№ док.	Подп.	Дата
Разраб.		Кырлан А.С.			21.10.26
Пров.					
ГИП					
Н. контр.					
Утв.					

ГД-2026-011-АИ

Квартира 56 м²

ЖК «Северный парк», Москва

Дизайн-проект интерьера

Стадия	Лист	Листов
РП	72	83

Развёртка стены Г. Санузел (пом. 4)

М 1:20

Кырлан Александр Сергеевич


выпуск 19.10.2026 № 1c3e34763b · стр. 83 из 117

ПРЕДВАРИТЕЛЬНО · не для производства работ · открыто пунктов: 10 (реестр — л. 5)

Развёртки стен А, Б. Прихожая (пом. 5)

Прихожая (пом. 5) · вид изнутри помещения · размеры в мм, отметки в м

Развёртка стены А

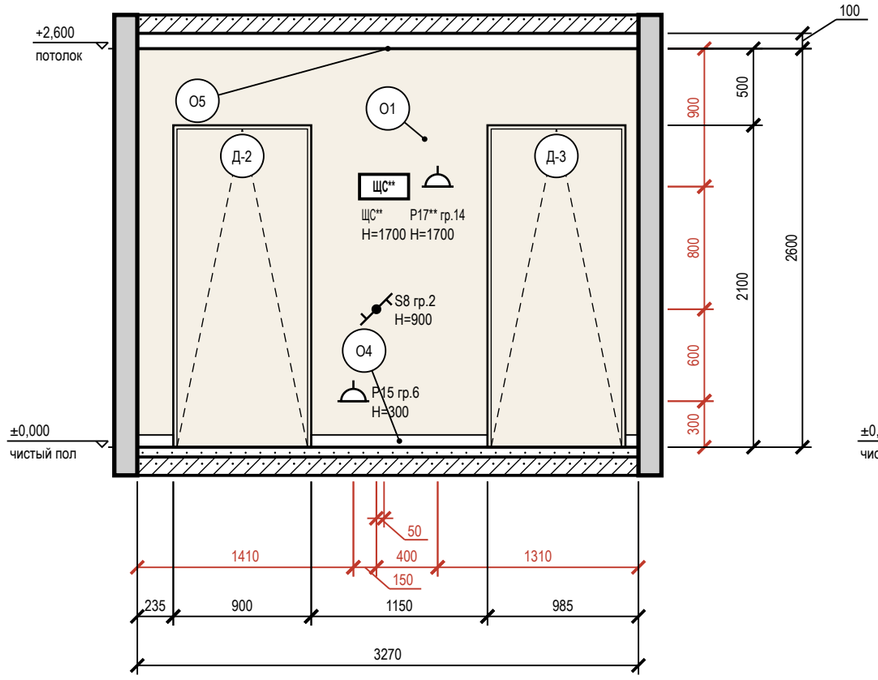

Развёртка стены Б


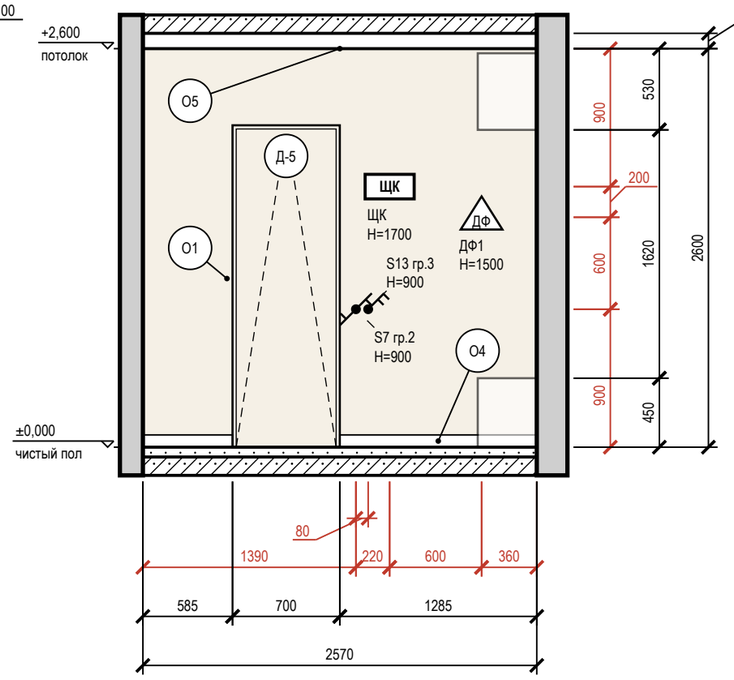


Схема развёрток (М 1:100)

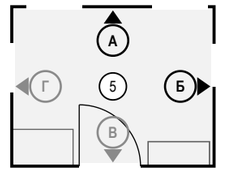

Условные обозначения

- розетка с заземляющим контактом; у знака — марка, ×N постов в рамке, гр. — группа щита, Н — высота оси, мм
- выключатель одноклавишный
- выключатель двухклавишный (флажков — по числу клавиш)
- выключатель с проходной или перекрёстной клавишей (обратный флажок); тип клавиши — в подписи
- ДФ — трубка или монитор домофона
- ЩК — щит квартирный
- привязки точек и выводов от угла и от пола, мм
- мебель и приборы — фасад по расстановке (условно)
- дверь скрытого монтажа: полотно в плоскости стены (узел — на листе узлов)
- стены и перекрытия в сечении
- окраска: тон — цвет по коду производителя (условно)
- О1 — марка отделки по реестру отделки альбома
- А — марка развёртки: буква стены, стрелка — взгляд

Ведомость отделки (на листе)

Марка	Поверхность	Материал, изделие	Цвет, код	Кол.
О1	стены	окраска, Tikkurila Euro Power 7, колеровка по NCS, матовая, подготовка Q3	NCS S 0804-Y30R «S 0804-Y30R»	9,9 м²
О4	плинтус	плинтус МДФ, h 80 мм, аналог: плинтус МДФ под покраску 80×16	NCS S 0804-Y30R «S 0804-Y30R»	3,3 м
О5	потолок	окраска, Tikkurila Euro Power 7, глубокоматовая, подготовка Q3	Tikkurila F485 «Damask»	8,6 м²

Допущения и предложения на листе

Основа листа: размеры помещений и положение проёмов введены заказчиком в брифе, на объекте не замерены (К-1); высота потолка 2700 мм — по брифу заказчика, не замерена (К-2); толщины стен приняты по брифу: наружные 200 мм, внутренние 150 мм — не обмерены (К-1); тип дома монолитный, перекрытие 200 мм — по брифу заказчика, документов нет (К-3); планировка (стены, проёмы, объединение кухни и гостиной, расширение санузла) — по брифу без обмера и плана БТИ (К-7); разрешённая мощность 10 кВт принята, ТУ не переданы (К-8); вентканалы приняты, в брифе не заданы (К-9); подрайон климата не задан — принят не северный (жилые от 2,5 м) (К-10).

Знак «*» — принято, не замерено и не подтверждено (замерить на объекте): К-1: дверь пом. 5 (стена В) — входная дверь: положение и ширина проёма — по брифу заказчика, не замерены.

Знак «**» — предложение проектировщика, заказчиком не утверждено (согласовать с заказчиком): записи в реестре нет: Р17 — высота 1700 мм выше нормы 1 м (ПУЭ 6.6.30) по назначению: питание слаботочного щита ЩС, рядом со щитом на его высоте; ЩС — щит слаботочный: место и состав.

См. лист открытых вопросов (лист 5, записи К-1–К-3, К-7–К-10).

Примечания

1. Развёртки — вид на стену изнутри помещения, по часовой стрелке; расположение — на схеме листа и на листе 62; размеры — в мм по чистовым поверхностям; отметки — в м от ±0,000; высоты Н — от чистого пола помещения до оси изделия, у декора — до центра.
2. Красные цепочки — привязки электроточек и выводов: по горизонтали от угла чистовых стен, по вертикали от чистого пола, до оси изделия; звенья короче 3 мм на листе вынесены во второй ярус (ближняя к стене цепочка).
3. У знака электроточки: марка (Р — розетка, S — выключатель, Св — светильник, ЭВ — вывод кабеля), ×N — число постов в рамке, гр. — группа щита, Н — высота оси от чистого пола, мм; группы по клавишам выключателя — на листе выключателей.
4. Схема мебели, приборов и декора не является технической документацией для производства мебели; габариты — по паспортам изделий.
5. Двери скрытого монтажа — полотно в плоскости стены, отделка стены по полотну, плинтус прерывается у короба (узел — на листе узлов).

1000 мм · печать 1:1


						ГД-2026-011-АИ	
						Квартира 56 м²	
						ЖК «Северный парк», Москва	
Изм.	Кол.уч	Лист	№ док.	Подп.	Дата		
Разраб.		Кырлан А.С.			21.10.26	Дизайн-проект интерьера	Стадия: РП; Лист: 73; Листов: 83
Пров.							
ГИП							
						Развёртки стен А, Б. Прихожая (пом. 5)	Кырлан Александр Сергеевич
Н. контр.						М 1:40	
Утв.							

выпуск 19.10.2026 № 1c3e34763b · стр. 84 из 117

Развёртки стен В, Г. Прихожая (пом. 5)

Прихожая (пом. 5) · вид изнутри помещения · размеры в мм, отметки в м

Развёртка стены В

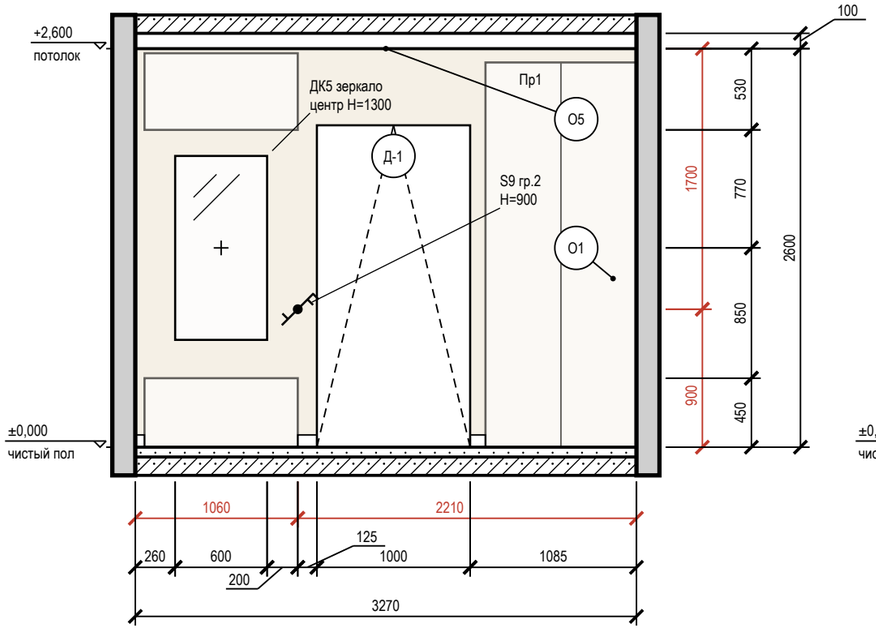

Развёртка стены Г


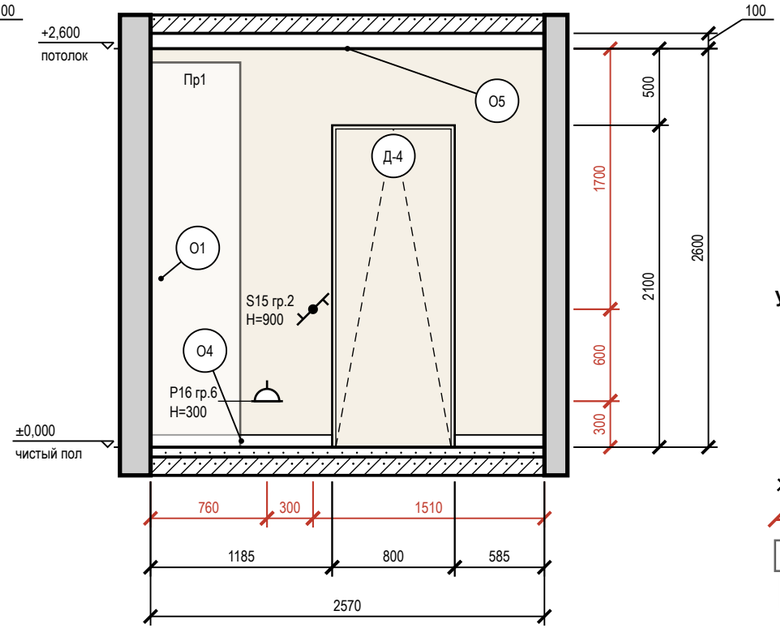


Схема развёрток (М 1:100)

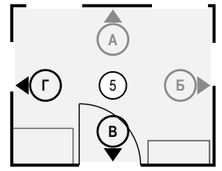

Условные обозначения

- розетка с заземляющим контактом; у знака — марка, ×N постов в рамке, гр. — группа щита, Н — высота оси, мм
- выключатель одноклавишный
- выключатель двухклавишный (флажков — по числу клавиш)
- выключатель с проходной или перекрёстной клавишей (обратный флажок); тип клавиши — в подписи
- привязки точек и выводов от угла и от пола, мм
- мебель и приборы — фасад по расстановке (условно)
- зеркало: марка Д, крест — центр, Н — высота центра, мм
- дверь скрытого монтажа: полотно в плоскости стены (узел — на листе узлов)
- дверной проём; марка двери — в кружке
- стены и перекрытия в сечении
- окраска: тон — цвет по коду производителя (условно)
- О1 — марка отделки по реестру отделки альбома
- А — марка развёртки: буква стены, стрелка — взгляд

Ведомость отделки (на листе)

Марка	Поверхность	Материал, изделие	Цвет, код	Кол.
О1	стены	окраска, Tikkurila Euro Power 7, колеровка по NCS, матовая, подготовка Q3	NCS S 0804-Y30R «S 0804-Y30R»	11,4 м²
О4	плинтус	плинтус МДФ, h 80 мм, аналог: плинтус МДФ под покраску 80×16	NCS S 0804-Y30R «S 0804-Y30R»	2,1 м
О5	потолок	окраска, Tikkurila Euro Power 7, глубокоматовая, подготовка Q3	Tikkurila F485 «Damask»	8,6 м²

Допущения и предложения на листе

Основа листа: размеры помещений и положение проёмов введены заказчиком в брифе, на объекте не замерены (К-1); высота потолка 2700 мм — по брифу заказчика, не замерена (К-2); толщины стен приняты по брифу: наружные 200 мм, внутренние 150 мм — не обмерены (К-1); тип дома монолитный, перекрытие 200 мм — по брифу заказчика, документов нет (К-3); планировка (стены, проёмы, объединение кухни и гостиной, расширение санузла) — по брифу без обмера и плана БТИ (К-7); разрешённая мощность 10 кВт принята, ТУ не переданы (К-8); вентканалы приняты, в брифе не заданы (К-9); подрайон климата не задан — принят не северный (жилые от 2,5 м) (К-10).

Знак «*» — принято, не замерено и не подтверждено (замерить на объекте): К-1: дверь пом. 5 (стена В) — входная дверь: положение и ширина проёма — по брифу заказчика, не замерены.

См. лист открытых вопросов (лист 5, записи К-1–К-3, К-7–К-10).

Примечания

1. Развёртки — вид на стену изнутри помещения, по часовой стрелке; расположение — на схеме листа и на листе 62; размеры — в мм по чистовым поверхностям; отметки — в м от ±0,000; высоты Н — от чистого пола помещения до оси изделия, у декора — до центра.
2. Красные цепочки — привязки электроточек и выводов: по горизонтали от угла чистовых стен, по вертикали от чистого пола, до оси изделия; звенья короче 3 мм на листе вынесены во второй ярус (ближняя к стене цепочка).
3. У знака электроточки: марка (Р — розетка, S — выключатель, Св — светильник, ЭВ — вывод кабеля), ×N — число постов в рамке, гр. — группа щита, Н — высота оси от чистого пола, мм; группы по клавишам выключателя — на листе выключателей.
4. Схема мебели, приборов и декора не является технической документацией для производства мебели; габариты — по паспортам изделий.
5. Картины и зеркала крепить к основанию по паспорту изделия (закладные и анкеры — в перечне скрытых работ); крест — ось центра предмета.
6. Двери скрытого монтажа — полотно в плоскости стены, отделка стены по полотну, плинтус прерывается у короба (узел — на листе узлов).

1000 мм · печать 1:1

Изм.	Кол.уч	Лист	№ док.	Подп.	Дата
Разраб.		Кырлан А.С.			21.10.26
Пров.					
ГИП					
Н. контр.					
Утв.					

ГД-2026-011-АИ

Квартира 56 м²

ЖК «Северный парк», Москва

Дизайн-проект интерьера

Стадия	Лист	Листов
РП	74	83

Развёртки стен В, Г. Прихожая (пом. 5)

М 1:40

Кырлан Александр Сергеевич


выпуск 19.10.2026 № 1c3e34763b · стр. 85 из 117

Узлы

Пороги и стыки покрытий, скрытые двери, короба стояков, гидроизоляция, плинтус


1 Порог 15 мм: мокрая зона — жилое помещение (М 1:10)

Применение: двери Д-5; места — лист 62

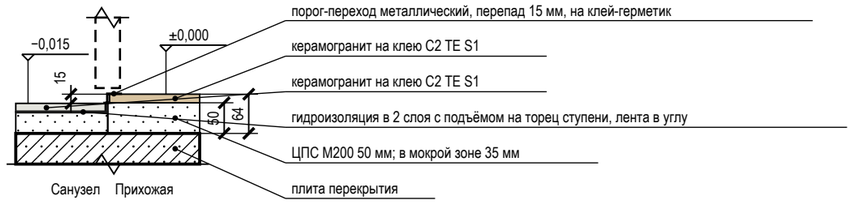


2 Стык покрытий пола Т-профилем без перепада (М 1:5)

Применение: проёмы 1↔5, 2↔5, 3↔5; места — лист 62

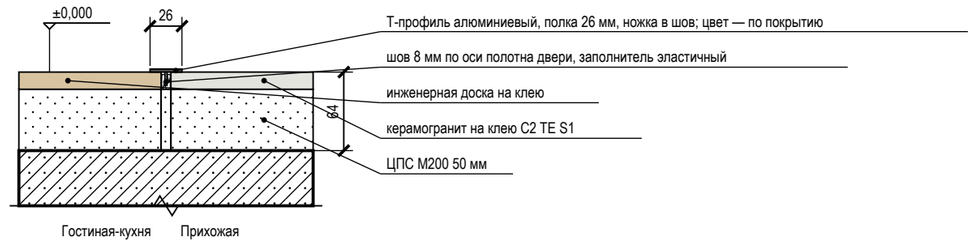


3 Дверь скрытого монтажа в плоскости стены, плинтус (М 1:5)

Применение: двери Д-2, Д-3, Д-4, Д-5; места — лист 62

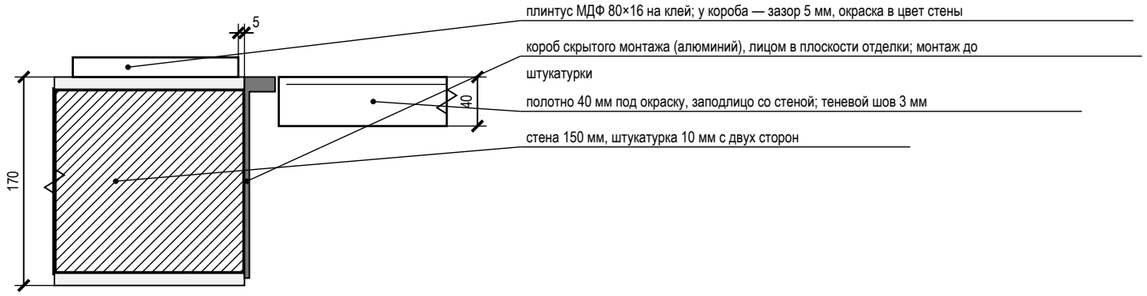


4 Короб стояков К1-1 с люком и звукоизоляцией (М 1:20)

Применение: пом. 4; места — лист 62

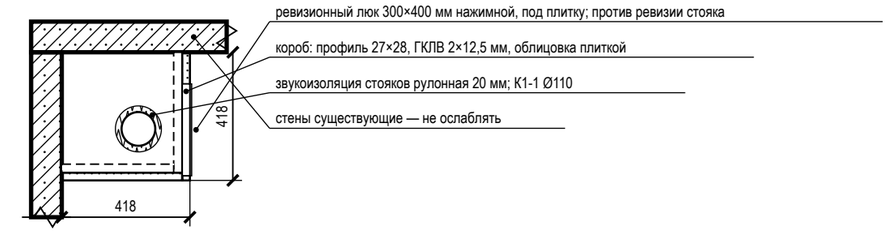


5 Гидроизоляция санузла: заход на стены 200 мм, примыкание ванны (М 1:20)

Применение: пом. 4; места — лист 62

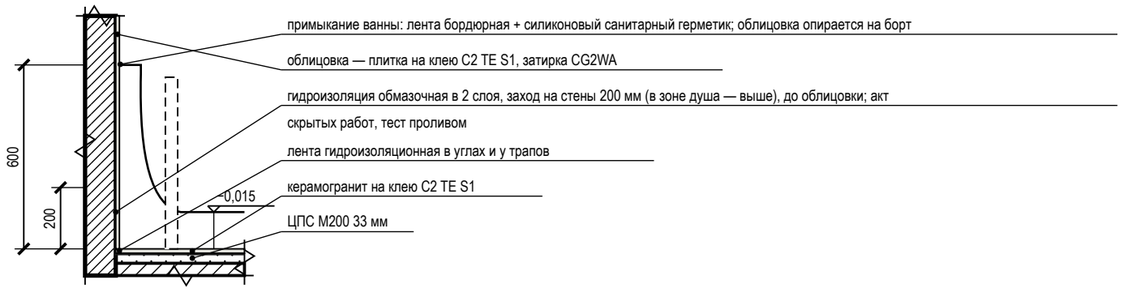

6 Плинтус МДФ 80×16 мм у окрашенной стены (М 1:10)

Применение: пом. 1, 2, 3, 5; места — лист 62

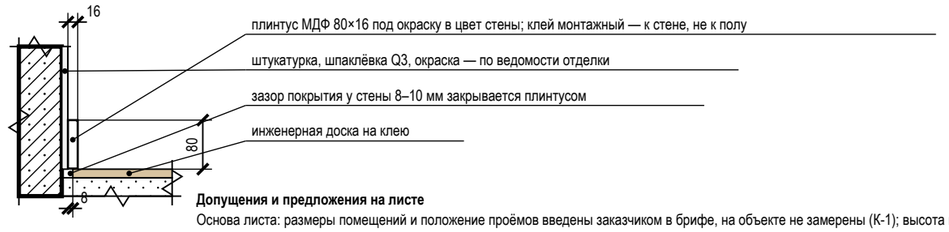

Допущения и предложения на листе

Основа листа: размеры помещений и положение проёмов введены заказчиком в брифе, на объекте не замерены (К-1); высота потолка 2700 мм — по брифу заказчика, не замерена (К-2); толщины стен приняты по брифу: наружные 200 мм, внутренние 150 мм — не обмерены (К-1); тип дома монолитный, перекрытие 200 мм — по брифу заказчика, документов нет (К-3); планировка (стены, проёмы, объединение кухни и гостиной, расширение санузла) — по брифу без обмера и плана БТИ (К-7); разрешённая мощность 10 кВт принята, ТУ не переданы (К-8); вентканалы приняты, в брифе не заданы (К-9); подрайон климата не задан — принят не северный (жилые от 2,5 м) (К-10).

См. лист открытых вопросов (лист 5, записи К-1–К-3, К-7–К-10).

Условные обозначения

- железобетон (плита, стены)
- кладка, перегородка
- стяжка, раствор
- гипсокартон ГКЛВ
- звукоизоляция, эластичный заполнитель
- плитка, керамогранит на клею
- инженерная доска (покрытие пола)
- металлический профиль (порог, Т-профиль, короб двери)
- гидроизоляция (обмазочная, лента)

Примечания

1. Узлы — типовые решения проекта для мест, отмеченных выносками на листе схемы расположения развёрток и узлов; размеры — в мм, отметки — в м от ±0,000.
2. Узлы с гидроизоляцией, закладными и коробами скрытого монтажа принимаются по актам скрытых работ до закрытия отделкой; гидроизоляция — после теста проливом (24 ч).
3. Марки изделий (порог, Т-профиль, короб скрытой двери, люк) — по спецификациям; замена — на аналог с теми же габаритами по согласованию с автором проекта.

Изм.	Кол.уч	Лист	№ док.	Подп.	Дата
Разраб.		Кырлан А.С.			21.10.26
Пров.					
ГИП					
Н. контр.					
Утв.					

ГД-2026-011-АИ

Квартира 56 м²

ЖК «Северный парк», Москва

Дизайн-проект интерьера

Стадия	Лист	Листов
РП	75	83

Узлы

М б/м

Кырлан Александр Сергеевич

выпуск 19.10.2026 № 1c3e34763b · стр. 86 из 117

10

Смета

Кырлан Александр Сергеевич

выпуск 19.10.2026 · 1c3e34763b · стр. 87 из 117

Ведомость объёмов работ

ПРЕДВАРИТЕЛЬНО · не для производства работ · открыто пунктов: 10 (реестр — л. 5)

Объёмы по помещениям от чертежа · площади в м², длины в м · формула, правило проёмов и источник в каждой строке

Ведомость объёмов работ по помещениям

Поз.	Наименование работ (материал, число слоёв)	Ед. изм.	Объём по помещениям (№ по экспликации)					Всего	Формула подсчёта	Правило проёмов	Источник	Цена за ед., ₽	Стоимость, ₽
			1	2	3	4	5						
1. Демонтаж и черновые работы													
1	Демонтаж существующего покрытия пола до основания	м²	20,80	13,60	8,58	4,81	8,58	56,37	S пом.		л. 13, 14	по КП	
2	Демонтаж существующей отделки стен до основания	м²	43,25	32,94	25,79	21,80	21,65	145,43	P × H − проёмы	за вычетом проёмов	л. 13, 14	по КП	
3	Демонтаж существующей отделки потолка до основания	м²	20,80	13,60	8,58	4,81	8,58	56,37	S пом.		л. 13, 14	по КП	
4	Демонтаж существующих дверных блоков	шт	1	1	1	1	1	5	по ведомости проёмов		л. 14, 15	по КП	
5	Демонтаж существующих сантехприборов и электрооборудования (если есть)	компл							по факту на объекте		л. 14	по КП	
6	Кладка перегородки П-1** (блоки, толщина 100 мм): Пеноблок D500, армирование через 2 ряда, штукатурка с двух сторон; предложение, пока П-1** не утверждена автором (К-5)	м²						5,55	2,60 × 2,70 − 1,47 (Д-5 700 × 2100) = 5,55 м², одна сторона; объём 0,56 м³; пом. 4, 5	проёмы вычтены	л. 14	по КП	
7	Кладка перегородки П-3** (кирпич, толщина 120 мм): Кирпич керамический полнотелый на ребро, штукатурка с двух сторон; предложение, пока П-3** не утверждена автором (К-5)	м²						10,80	4,00 × 2,70 = 10,80 м², одна сторона; объём 1,3 м³; пом. 1, 2	проёмы вычтены	л. 14	по КП	
8	Устройство перемычек над проёмами в кладке П-1**; предложение, пока П-1** не утверждена автором (К-5)	шт						1	проём Д-5 700 мм → перемычка 1200 мм (опирание 250 мм с каждой стороны — принято, практика)		л. 14	по КП	
9	Монтаж каркасной перегородки П-2** (С112): каркас ПС усиленный через 600 мм, ГКЛ в 2 слоя с каждой стороны, обрамление проёма профилем УА; предложение, пока П-2** не утверждена автором (К-5)	м²						5,34	2,60 × 2,70 − 1,68 (Д-4 800 × 2100) = 5,34 м², одна сторона; пом. 3, 5	проёмы вычтены	л. 14, 35	2 700	14 418
10	Заполнение каркаса П-2** минераловатной плитой (звукоизоляция, Rw 51 дБ); предложение, пока П-2** не утверждена автором (К-5)	м²						5,34	5,34 м² без проёма		л. 35	по КП	
11	Устройство стяжки: стяжка ЦПС М200, 50 мм	м²	20,87	13,67	8,64	4,86	8,93	56,97	S пом. + S в дверных проёмах (b × t/2)	проёмы добавлены	л. 43, 44	530	30 194
12	Гидроизоляция обмазочная, 2 слоя: пол, стены на 200 мм, зоны замачивания	м²				11,29		11,29	пол + (P − двери) × h заведения + зоны замачивания		л. 40	450	5 081
13	Штукатурка стен по маякам, до 10 мм	м²	43,25	32,94	20,45	21,80	16,31	134,75	P × H − проёмы по обводу коробок − грани перегородок на ГКЛВ	за вычетом проёмов	л. 13, 44	530	71 418
14	Штукатурка оконных откосов шириной до 200 мм	м²	0,62	0,57	0,56			1,75	Σ (2h + b) × глубина откоса	откосы ≤ 200 мм	л. 13	540	945
15	Потолок ГКЛ по каркасу П113, 1 слой	м²	20,80	13,60	8,58	4,81	8,58	56,37	S пом. по плану потолков		л. 36–39	1 500	84 555
Итого по разделу 1 — 206 611 ₽ (позиций 15, из них по КП 9); в сводную смету — л. 82, 83													
2. Инженерные системы													
16	Прокладка кабеля ВВГнг(A)-LS по группам щита: за потолком и в штробах стен (штробы — только после технического заключения, см. строку «Штробы в стенах»)	м						386,00	Σ длин групп щита		л. 26	60	23 160
17	Прокладка слаботочной линии: Кабель домофона — тип по системе поставщика, отдельно от силовых	м						6,70	по лучам от ЩС**: 1 точ., запас 10 %		л. 28	по КП	
18	Прокладка слаботочной линии: Кабель коаксиальный RG-6 (75 Ом) к розеткам ТВ, отдельно от силовых	м						11,70	по лучам от ЩС**: 1 точ., запас 10 %		л. 28	по КП	
19	Прокладка слаботочной линии: Кабель U/UTP кат. 6 (LAN, Wi-Fi и камеры по PoE), отдельно от силовых	м						46,50	по лучам от ЩС**: 5 точ., запас 10 %		л. 28	по КП	
20	Прокладка гофротрубы Ø20 для слаботочных линий, отдельно от силовых	м						58,40	по длине лучей без участков в канале плинтуса (≈ 90 %)		л. 28	по КП	
21	Сборка слаботочного щита ЩС**: корпус, патч-панель, подключение линий и питания 220 В; коммутатор и точки доступа — оборудование заказчика	шт						1	один щит		л. 24, 25, 28	по КП	
22	Электроточка: подрозетник в бетоне, розетка, выключатель, вывод	шт	24	10	9	4	10	57	по ведомости электроточек		л. 21, 24, 25	950	54 150

Допущения и предложения на листе

Основа листа: размеры помещений и положение проёмов введены заказчиком в брифе, на объекте не замерены (К-1); высота потолка 2700 мм — по брифу заказчика, не замерена (К-2); толщины стен приняты по брифу: наружные 200 мм, внутренние 150 мм — не обмерены (К-1); тип дома монолитный, перекрытие 200 мм — по брифу заказчика, документов нет (К-3); планировка (стены, проёмы, объединение кухни и гостиной, расширение санузла) — по брифу без обмера и плана БТИ (К-7); разрешённая мощность 10 кВт принята, ТУ не переданы (К-8); вентканалы приняты, в брифе не заданы (К-9); подрайон климата не задан — принят не северный (жилые от 2,5 м) (К-10).

Знак «**» — предложение проектировщика, заказчиком не утверждено (согласовать с заказчиком): К-5: П-1 — положение, материал (пеноблок) и толщина 100 мм — по брифу заказчика; конструкция (кладка, армирование, штукатурка) — выбор исполнителя, автором не утверждена; кладка — не ГКЛ: каркас, листы и Rw системы не считаются (система, лист, слои, Rw — «—»); П-2 — положение, материал (ГКЛ) и толщина 150 мм — по брифу заказчика; конструкция (система С112, 2 слоя с каждой стороны, Rw 51 дБ — нижняя граница диапазона системы С112 (51–56 дБ)) — выбор исполнителя, автором не утверждена; П-3 — положение, материал (кирпич) и толщина 120 мм — по брифу заказчика; конструкция (кладка, армирование, штукатурка) — выбор исполнителя, автором не утверждена; кладка — не ГКЛ: каркас, листы и Rw системы не считаются (система, лист, слои, Rw — «—»); записи в реестре нет: ЩС — щит слаботочный: место и состав.

См. лист открытых вопросов (лист 5, записи К-1–К-3, К-5, К-7–К-10).

Изм.	Кол.уч	Лист	№ док.	Подп.	Дата
Разраб.		Кырлан А.С.			21.10.26
Пров.					
ГИП					
Н. контр.					
Утв.					

ГД-2026-011-АИ

Квартира 56 м²

ЖК «Северный парк», Москва

Дизайн-проект интерьера

Стадия	Лист	Листов
РП	76	83

Ведомость объёмов работ

М б/м

Кырлан Александр Сергеевич

Ведомость объёмов работ (продолжение)

Объёмы по помещениям от чертежа · площади в м², длины в м · формула, правило проёмов и источник в каждой строке

Ведомость объёмов работ по помещениям (продолжение)

Поз.	Наименование работ (материал, число слоёв)	Ед. изм.	Объём по помещениям (№ по экспликации)					Всего	Формула подсчёта	Правило проёмов	Источник	Цена за ед., ₽	Стоимость, ₽
			1	2	3	4	5						
23	Штробы в стенах под спуски кабеля к точкам — выполняются только после технического заключения о несущих стенах	м	39,35	18,00	16,40	5,16	15,10	94,01	Σ (H − h) по точкам на стенах: вертикальные спуски	после техзаключения	л. 14, 21	по КП	
24	Установка встраиваемого точечного светильника	шт	12	8	6	3	4	33	по плану освещения		л. 22	750	24 750
25	Монтаж светильника: потолочного, подвесного, настенного	шт	3	2	2	1		8	по плану освещения		л. 22	1 200	9 600
26	Монтаж LED-ленты в алюминиевый профиль	м	9,40	11,70	8,70		1,80	31,60	Σ длин лент по плану освещения		л. 22	230	7 268
27	Установка блока питания LED в доступном месте (люк, шкаф)	шт	2	1	1		1	5	один на LED-группу		л. 22	570	2 850
28	Установка автономного пожарного извещателя	шт	2	1	1		1	5	по плану розеток		л. 21	по КП	
29	Сборка щита: установка автоматов и АВДТ групп, вводного автомата	шт						15	группы + вводной автомат		л. 26	230	3 450
30	Установка вводного УЗО	шт						1	по однолинейной схеме		л. 26	380	380
31	Монтаж инсталляции, установка подвесного унитаза и кнопки смыва	шт				1		1	по плану выводов		л. 31, 33	10 500	10 500
32	Короб инсталляции: каркас и обшивка ГКЛВ в 2 слоя, ревизионный доступ к смыву	шт				1		1	по плану выводов		л. 31, 40–42	по КП	
33	Короб К1 над чистым полом: каркас и обшивка ГКЛВ под плитку (материалы — в спецификации ВК)	м.п.	10,68			3,86		14,54	Σ открытых участков выпусков К1 (профиль листа разводки ВК)		л. 31, 33	по КП	
34	Установка ванны с сифоном	шт				1		1	по плану выводов		л. 31, 33	6 000	6 000
35	Установка умывальника (мойки) с сифоном и смесителем	шт	1			1		2	по плану выводов		л. 31, 33	3 000	6 000
36	Подключение стиральной (посудомоечной) машины к ВК	шт	1			1		2	по плану выводов		л. 31	по КП	
37	Установка радиатора с узлом подключения и терморегулятором	шт	1	1	1			3	по плану отопления		л. 30	по КП	
Итого по разделу 2 — 148 108 ₽ (позиций 22, из них по КП 11); в сводную смету — л. 82, 83													
3. Чистовые работы													
38	Облицовка стен керамогранитом 600×1200 на клею	м²				18,97		18,97	по раскладке: зона облицовки − место за коробом	за вычетом проёмов	л. 40–42	2 500	47 425
39	Облицовка короба инсталляции (ГКЛВ) керамогранитом: лицо, боковины, полка	м²				1,76		1,76	по раскладке: лицо, боковины, полка		л. 40–42	2 500	4 400
40	Облицовка фартука керамогранитом 1200×600	м²	1,82					1,82	по раскладке фартука		л. 40–42, 44	2 400	4 368
41	Укладка керамогранита на пол, 600×1200, на клею	м²				4,86	8,93	13,79	S пом. + S в дверных проёмах	проёмы добавлены	л. 40–43	1 800	24 822
42	Затирка швов керамогранита	м²	1,82			25,54	8,58	35,94	Σ S облицовки и пола из плитки		л. 40–42	150	5 391
43	Грунтование стен, 2 слоя (под штукатурку и под отделку)	м²	43,25	32,94	25,79	21,80	21,65	145,43	P × H − проёмы	за вычетом проёмов	л. 44	96	13 961
44	Шпаклёвка стен под окраску, 2 слоя (старт и финиш), уровень Q3	м²	41,43	32,94	25,79		21,65	121,81	P × H − проёмы − фартук	за вычетом проёмов	л. 44	750	91 358
45	Грунтование и шпаклёвка оконных откосов, 2 слоя	м.п.	4,80	4,40	4,30			13,50	Σ (2h + b) по окнам	по окнам	л. 13	300	4 050
46	Грунтование потолка, 2 слоя	м²	20,80	13,60	8,58	4,81	8,58	56,37	S пом.		л. 44	96	5 412
47	Шпаклёвка потолка под окраску, 2 слоя, уровень Q3	м²	20,80	13,60	8,58	4,81	8,58	56,37	S пом.		л. 36–39, 44	950	53 552
48	Окраска потолка водно-дисперсионной краской, 2 слоя	м²	20,80	13,60	8,58	4,81	8,58	56,37	S пом.		л. 44	360	20 293
49	Окраска стен водно-дисперсионной краской, 2 слоя	м²	46,02	37,00	29,50		30,68	143,20	P × H − фартук, проёмы не вычитаются	без вычета проёмов	л. 44	300	42 960
50	Окраска оконных откосов, 2 слоя	м.п.	4,80	4,40	4,30			13,50	Σ (2h + b) по окнам	по окнам	л. 13	120	1 620

Допущения и предложения на листе

Основа листа: размеры помещений и положение проёмов введены заказчиком в брифе, на объекте не замерены (К-1); высота потолка 2700 мм — по брифу заказчика, не замерена (К-2); толщины стен приняты по брифу: наружные 200 мм, внутренние 150 мм — не обмерены (К-1); тип дома монолитный, перекрытие 200 мм — по брифу заказчика, документов нет (К-3); планировка (стены, проёмы, объединение кухни и гостиной, расширение санузла) — по брифу без обмера и плана БТИ (К-7); разрешённая мощность 10 кВт принята, ТУ не переданы (К-8); вентканалы приняты, в брифе не заданы (К-9); подрайон климата не задан — принят не северный (жилые от 2,5 м) (К-10).

См. лист открытых вопросов (лист 5, записи К-1–К-3, К-7–К-10).

Изм.	Кол.уч	Лист	№ док.	Подп.	Дата
Разраб.		Кырлан А.С.			21.10.26
Пров.					
ГИП					
Н. контр.					
Утв.					

ГД-2026-011-АИ

Квартира 56 м²

ЖК «Северный парк», Москва

Дизайн-проект интерьера

Стадия	Лист	Листов
РП	77	83

Ведомость объёмов работ (продолжение)

М б/м

Кырлан Александр Сергеевич

Ведомость объёмов работ (окончание)

Объёмы по помещениям от чертежа · площади в м², длины в м · формула, правило проёмов и источник в каждой строке

Ведомость объёмов работ по помещениям (продолжение)

Поз.	Наименование работ (материал, число слоёв)	Ед. изм.	Объём по помещениям (№ по экспликации)					Всего	Формула подсчёта	Правило проёмов	Источник	Цена за ед., ₽	Стоимость, ₽
			1	2	3	4	5						
51	Укладка инженерной доски на клей	м²	20,87	13,67	8,64			43,18	S пом. + S в дверных проёмах	проёмы добавлены	л. 43, 44	1 200	51 816
52	Установка плинтуса МДФ h=80 мм	м.п.	17,50	13,90	11,00		7,50	49,90	P − ширина дверных проёмов		л. 44	450	22 455
53	Окраска плинтуса в тоне S 0804-Y30R, 2 слоя	м.п.	17,50	13,90	11,00		7,50	49,90	как плинтус		л. 44	300	14 970
54	Монтаж дверей скрытого монтажа под покраску (поставщик дверей)	шт	1	1	1	1		4	по ведомости проёмов		л. 15	5 250	21 000
55	Входная дверь, поставка с монтажом и откосами	шт						1	по ведомости проёмов		л. 15	по КП	
Итого по разделу 3 — 429 853 ₽ (позиций 18, из них по КП 1); в сводную смету — л. 82, 83													

Ведомость подсчёта площадей по помещениям

№	Помещение	S пола, м²	P, м	H, м	P × H, м²	Проёмы, м²	Стены нетто, м²	В дверных проёмах, м²	Плинтус, м	Откосы, м.п.
1	Гостиная-кухня	20,80	18,40	2,60	47,84	4,59	43,25	0,07	17,50	4,80
2	Спальня	13,60	14,80	2,50	37,00	4,07	32,94	0,07	13,90	4,40
3	Детская	8,58	11,80	2,50	29,50	3,71	25,79	0,06	11,00	4,30
4	Санузел	4,81	8,90	2,62	23,27	1,47	21,80	0,05	нет	нет
5	Прихожая	8,58	11,80	2,60	30,68	9,03	21,65	0,35	7,50	нет
	Итого	**56,37**			**168,29**	**22,87**	**145,43**	**0,59**	**49,90**	**13,50**

Реестр контрольных сумм

Показатель	По ВОР	По чертежу	Расхождение	Лист
Σ площадей помещений без летних, м² — общая площадь по экспликации	56,37	56,37	0,0 %	л. 13
Стены под окраску, м² (шпаклёвка) ведомость отделки	121,81	121,81	0,0 %	л. 44
Потолки под окраску, м² — ведомость отделки	56,37	56,37	0,0 %	л. 44
Плинтус, м — ведомость отделки	49,90	49,90	0,0 %	л. 44
Плитка к заказу, шт — ведомость плитки	86	86	0,0 %	л. 40
Гидроизоляция, м² — ведомость материалов плитки	11,29	11,29	0,0 %	л. 40
Точки ЭОМ, шт — планы ЭОМ (без щитов)	113	114	-0,9 %	л. 21, 22

Примечания

1. Объёмы — от геометрии проекта (та же, что на планах и в ведомости отделки), не от общей площади: P — периметр чистого контура, H — от чистого пола до низа потолка, проёмы — по наружному обводу коробок.
2. Подсчёт по ГЭСН-2001-15 и ГЭСН-2001-11: штукатурка и шпаклёвка стен — за вычетом проёмов; окраска водными составами — без вычета проёмов (п. 2.24); откосы — отдельно, по ширине до 200 и более 200 мм; полы — с площадью в дверных проёмах.
3. Плитка — по раскладке (целые и с подрезкой); короб инсталляции и фартук — отдельными строками, двойного счёта облицовки нет. Материалы, запас и количество к заказу — в спецификации материалов.
4. Цены — ориентир по открытым прайсам Москвы (прайсы собраны 21.09.2026, часть расценок сверена повторно 06.10.2026), не коммерческое предложение; «по КП» — расценки нет, строка в итог не входит.
5. Демонтаж — по плану демонтажа и общим указаниям: покрытия пола, отделка стен и потолков, дверные блоки — до основания; объёмы справочные, уточняются по факту на объекте (расценки в книге нет — «по КП»).
6. Штробы в стенах — только после технического заключения о несущих стенах (общие указания, план обмера и демонтажа): строка «Штробы в стенах» вертикальные спуски кабеля от потолочной трассы к точкам, объём не меньше фактического (горизонтальные трассы — по исполнительной схеме). Расценки штробления в прайсе нет — «по КП», в итог не входит; кабель в штробах стен прокладывается после неё.
7. Площадь облицовки стен — одно число с тремя названиями: зона облицовки по ведомости отделки 19,93 м² − место за коробом инсталляции 0,96 м² (плитку туда не кладут) = стены под плитку 18,97 м² (строка «Облицовка стен»); облицовка коробов 1,76 м² — отдельной строкой; стены и короба вместе — 20,73 м² (столько плитки по раскладке в спецификации). Источник — один (quantities.js), расхождение на листах ловит.
8. Слаботочные сети: кабель по лучам от ЩС** 64,90 м (U/UTP, RG-6, домофон — по видам), гофра 58,40 м, щит ЩС** с патч-панелью; розетки RJ45 и ТВ монтируются в строке «Электроточка». Длины те же, что в ведомости изделий электрика (одна модель — lowcurrent-engineer/bom.js); оборудование заказчика (точки доступа, камеры, коммутатор) в спецификацию не входит. 2 точ. — предложение листа слаботочки.
9. Перегородки и облицовки ГКЛ (П-2** — 5,34 м²): площадь одной стороны за вычетом проёмов, из той же модели, по которой выпущена схема каркаса; обшивка, профиль и заполнение — в спецификации материалов. П-2** — предложение проектировщика, автором не утверждено: деньги заложены на решение, которое может измениться. Грани перегородок на ГКЛВ вычтены из штукатурки стен (10,68 м²): штукатурят основание, а не обшивку.
10. Перегородки из кладки (П-1** — 5,55 м², 0,56 м³, П-3** — 10,80 м², 1,3 м³): площадь одной стороны за вычетом проёмов, объём — площадь × толщина; перемычки — по одной на проём, длина — ширина + 2 × опирание (принятое опирание 250 мм — практика, СП 15.13330 его не задаёт). Изделия заказываются в м³, кладочная смесь — по ТУ производителя: расхода в источниках нет, число не ставится. Не посчитано: П-1**: размер изделия и толщина шва (masonry.unit, masonry.joint) в данных не заданы — число рядов и длина армирования не считаются; длина одного ряда — 1,9 м; П-1**: штуки изделий не считаются: размер блока в данных не задан — заказ в м³ (объём кладки); П-3**: размер изделия и толщина шва (masonry.unit, masonry.joint) в данных не заданы — число рядов не считается; длина одного ряда — 4 м; П-3**: штуки изделий не считаются: размер кирпича в данных не задан — заказ в м³ (объём кладки). Грани кладки штукатурят — они в строке штукатурки стен помещений. П-1**, П-3** — предложение проектировщика, автором не утверждено.
11. Коробы: стояков (нет) и К1 над чистым полом (14,54 м открытых участков; труба К1 вдоль стен 38,24 м в короб не зашивается — она за приборами, в раме инсталляции и в шахтах). В спецификации ВК короб К1 заказывается с запасом 10 % — 16,00 м. Материалы коробов стояков и инсталляции — в спецификации материалов, К1 — в спецификации ВК.

Допущения и предложения на листе

Основа листа: размеры помещений и положение проёмов введены заказчиком в брифе, на объекте не замерены (К-1); высота потолка 2700 мм — по брифу заказчика, не замерена (К-2); толщины стен приняты по брифу: наружные 200 мм, внутренние 150 мм — не обмерены (К-1); тип дома монолитный, перекрытие 200 мм — по брифу заказчика, документов нет (К-3); планировка (стены, проёмы, объединение кухни и гостиной, расширение санузла) — по брифу без обмера и плана БТИ (К-7); разрешённая мощность 10 кВт принята, ТУ не переданы (К-8); вентканалы приняты, в брифе не заданы (К-9); подрайон климата не задан — принят не северный (жилые от 2,5 м) (К-10).

Знак «**» — предложение проектировщика, заказчиком не утверждено (согласовать с заказчиком): К-5: П-1 — положение, материал (пеноблок) и толщина 100 мм — по брифу заказчика; конструкция (кладка, армирование, штукатурка) — выбор исполнителя, автором не утверждена; кладка — не ГКЛ: каркас, листы и Rw системы не считаются (система, лист, слои, Rw — «—»); П-2 — положение, материал (ГКЛ) и толщина 150 мм — по брифу заказчика; конструкция (система С112, 2 слоя с каждой стороны, Rw 51 дБ — нижняя граница диапазона системы С112 (51–56 дБ)) — выбор исполнителя, автором не утверждена; П-3 — положение, материал (кирпич) и толщина 120 мм — по брифу заказчика; конструкция (кладка, армирование, штукатурка) — выбор исполнителя, автором не утверждена; кладка — не ГКЛ: каркас, листы и Rw системы не считаются (система, лист, слои, Rw — «—»); записи в реестре нет: ЩС — щит слаботочный: место и состав.

См. лист открытых вопросов (лист 5, записи К-1–К-3, К-5, К-7–К-10).

Изм.	Кол.уч	Лист	№ док.	Подп.	Дата	ГД-2026-011-АИ		
						Квартира 56 м²		
						ЖК «Северный парк», Москва		
Разраб.		Кырлан А.С.			21.10.26	Дизайн-проект интерьера	Стадия	Лист	Листов
Пров.							РП	78	83
ГИП									
Н. контр.						Ведомость объёмов работ (окончание) М б/м	Кырлан Александр Сергеевич		
Утв.									

Спецификация материалов

Отделочные материалы: чистое количество, запас, упаковка, к заказу · ГОСТ 21.110-2013

Спецификация материалов (ГОСТ 21.110-2013, форма 1)

Поз.	Наименование и техническая характеристика	Тип, марка, артикул	Код продукции	Поставщик	Ед. изм.	Количество				Масса ед., кг	Примечание
						чистое	запас, %	упаковка	к заказу		
Покрытия полов и облицовка											
1	Инженерная доска (дуб натуральный, рабочий слой 4 мм, эмиссия E1, прямая укладка)	1167-1101			м²	43,18	7	по артикулу	46,20 м²		пом. 1, 2, 3; до целой упаковки; л. 43, 44
2	Клей для паркетной и инженерной доски (эластичный, по ТУ изготовителя доски)	по выбору подрядчика			м²	43,18		ведро по ТУ	по ТУ		расход кг/м² — по ТУ клея; л. 43
3	Керамогранит 600×600 мм под травертин	аналог: керамогранит под травертин			шт	15	10	коробка	17 шт		9 целых + 6 с подрезкой; 4,81 м² по раскладке, к заказу 6,12 м²; пом. 4; л. 40–42
4	Керамогранит 600×1200 мм под травертин	аналог: керамогранит под травертин			шт	38	10	коробка	43 шт		18 целых + 20 с подрезкой; 20,73 м² по раскладке, к заказу 30,96 м²; пом. 4; л. 40–42
5	Керамогранит 600×1200 мм A8UZ	A8UZ			шт	18	10	коробка	20 шт		4 целых + 14 с подрезкой; 8,58 м² по раскладке, к заказу 14,40 м²; пом. 5; л. 40–42
6	Керамогранит 1200×600 мм под травертин, матовый	аналог: керамогранит под травертин, матовый			шт	5	10	коробка	6 шт		0 целых + 5 с подрезкой; 1,82 м² по раскладке, к заказу 4,32 м²; пом. 1; л. 40–42
Сухие смеси и гидроизоляция											
7	Клей плиточный цементный класса C2 TE S1 (ГОСТ Р 56387-2018)	Ceresit CM 17 или аналог			кг	261,65	10	мешок 25 кг	12 меш.	25	слой 5 мм, 1,50 кг/м² на 1 мм; л. 40
8	Затирка цементная класса CG2WA, цвет — по колерной карте	Mapei Ultracolor Plus 132 или аналог			кг	2,62	10	упак. 2 кг	2 упак.	2	расход (a+b)/ab × шов × t × 1,6 кг/м²; л. 40
9	Гидроизоляция обмазочная полимерная, 2 слоя, лента в углах, манжеты на выводах	по выбору подрядчика			м²	11,29	10	ведро по ТУ	по ТУ		пом. 4; расход кг/м² — по ТУ; л. 40
10	Лента демпферная по периметру пола из плитки	по выбору подрядчика			м	15,39	10	рулон	17,00 м		л. 40
11	Смесь цементно-песчаная для стяжки М200 (50 мм, 33 мм)	по выбору подрядчика			м³	2,77	5	мешок по ТУ	по ТУ		S 56,97 м² × толщина; армирование и маяки — по ТУ; л. 43
12	Смесь штукатурная гипсовая для машинного и ручного нанесения по маякам, слой до 10 мм	по выбору подрядчика			м²	134,75	10	мешок по ТУ	по ТУ		пом. 1, 2, 3, 4, 5; расход кг/м² на 1 мм слоя — по ТУ смеси, толщина — по замеру кривизны стен; л. 13, 44
Короба из ГКЛВ											
13	Лист ГКЛВ 12,5 мм, 2500 × 1200 мм, обшивка коробов в 2 слоя	по выбору подрядчика			м²	3,52	10	лист 3,00 м²	2,00 лист		инсталляция пом. 4: 1,76 м²; площадь × 2 слоя; короб К1 над полом — в спецификации ВК; л. 31, 40–42
14	Профиль стальной оцинкованный 27 × 28 мм: каркас коробов (стойки и направляющие)	по выбору подрядчика			м	8,60	10	хлыст 3 м	4 шт		стойки через 400 мм по свободному периметру + направляющие по полу и потолку; крепёж, лента, шпаклёвка швов — по узлу короба; л. 31, 40–42
Перегородки и облицовки из ГКЛВ											
15	Лист ГКЛ 12,5 мм, 2500 × 1200 мм: обшивка перегородок и облицовок, 2 слоя на сторону	по выбору подрядчика			м²	21,36	10	лист 3,00 м²	8,00 лист		П-2**; площадь стороны × 2 слоя × стороны (проёмы вычтены); предложение, пока П-2** не утверждена автором (К-5); л. 14, 35
16	Профиль направляющий ПН 100: по потолку и полу, перемычки над проёмами	по выбору подрядчика			м	5,20	10	хлыст 3 м	2 шт		П-2**; ПН: шаг и положение стоек — на схеме каркаса; длина стойки равна высоте перегородки, стойки режут между направляющими при монтаже; предложение, пока П-2** не утверждена автором (К-5); л. 14, 35
17	Профиль стоечный ПС 100: стойки через шаг каркаса и короткие над проёмами	по выбору подрядчика			м	11,40	10	хлыст 3 м	5 шт		П-2**; ПС: шаг и положение стоек — на схеме каркаса; длина стойки равна высоте перегородки, стойки режут между направляющими при монтаже; предложение, пока П-2** не утверждена автором (К-5); л. 14, 35

Допущения и предложения на листе

Основа листа: размеры помещений и положение проёмов введены заказчиком в брифе, на объекте не замерены (К-1); высота потолка 2700 мм — по брифу заказчика, не замерена (К-2); толщины стен приняты по брифу: наружные 200 мм, внутренние 150 мм — не обмерены (К-1); тип дома монолитный, перекрытие 200 мм — по брифу заказчика, документов нет (К-3); планировка (стены, проёмы, объединение кухни и гостиной, расширение санузла) — по брифу без обмера и плана БТИ (К-7); разрешённая мощность 10 кВт принята, ТУ не переданы (К-8); вентканалы приняты, в брифе не заданы (К-9); подрайон климата не задан — принят не северный (жилые от 2,5 м) (К-10).

Знак «**» — предложение проектировщика, заказчиком не утверждено (согласовать с заказчиком): К-5: П-2 — положение, материал (ГКЛ) и толщина 150 мм — по брифу заказчика; конструкция (система С112, 2 слоя с каждой стороны, Rw 51 дБ — нижняя граница диапазона системы С112 (51–56 дБ)) — выбор исполнителя, автором не утверждена; записи в реестре нет: плинтус пом. 1, 2, 5, фартук пом. 1 — артикул изделия не выбран: позиция описана характеристиками («аналог по характеристикам»), артикул выбирается при закупке.

См. лист открытых вопросов (лист 5, записи К-1–К-3, К-5, К-7–К-10).

Изм.	Кол.уч	Лист	№ док.	Подп.	Дата
Разраб.		Кырлан А.С.			21.10.26
Пров.					
ГИП					
Н. контр.					
Утв.					

ГД-2026-011-АИ

Квартира 56 м²

ЖК «Северный парк», Москва

Дизайн-проект интерьера

Стадия	Лист	Листов
РП	79	83

Спецификация материалов

М б/м

Кырлан Александр Сергеевич

Спецификация материалов (продолжение)

Отделочные материалы: чистое количество, запас, упаковка, к заказу · ГОСТ 21.110-2013

Спецификация материалов (ГОСТ 21.110-2013, форма 1) (продолжение)

Поз.	Наименование и техническая характеристика	Тип, марка, артикул	Код продукции	Поставщик	Ед. изм.	Количество				Масса ед., кг	Примечание
						чистое	запас, %	упаковка	к заказу		
18	Профиль усиленный УА 100 (2,0 мм): стойки по краям проёма на полную высоту	по выбору подрядчика			м	5,40	10	хлыст 3 м	2 шт		П-2**; УА: шаг и положение стоек — на схеме каркаса; длина стойки равна высоте перегородки, стойки режут между направляющими при монтаже; предложение, пока П-2** не утверждена автором (К-5); л. 14, 35
19	Плита минераловатная звукопоглощающая в полость каркаса, толщина по глубине профиля 100 мм	по выбору подрядчика			м²	5,34	10	упаковка по ТУ	по ТУ		П-2**; заполнение принято (К-18): марка и плотность — при закупке; Rw системы нормируют с заполнением; предложение, пока П-2** не утверждена автором (К-5); л. 14, 35
20	Лента уплотнительная самоклеящаяся под профили по потолку, полу и у примыканий к стенам	по выбору подрядчика			м	9,80	10	рулон по ТУ	11,00 м		П-2**; по периметру каркаса: потолок, пол без проёма, крайние стойки у примыканий; предложение, пока П-2** не утверждена автором (К-5); л. 14, 35
21	Саморезы для ГКЛ по металлу (по слоям обшивки), дюбели для направляющих — по ТУ изготовителя системы	по выбору подрядчика			м²	21,36		упаковка по ТУ	по ТУ		П-2**; расход шт/м² и шаг дюбелей — по ТУ системы; считаются от площади обшивки; предложение, пока П-2** не утверждена автором (К-5); л. 14, 35
Перегородки из кладки											
22	Пеноблок D500: изделия кладки толщиной 100 мм	по выбору подрядчика			м³	0,56		поддон по ТУ	по ТУ		П-1**; объём кладки 5,55 м² × 100 мм (проёмы вычтены); размер изделия в данных не задан — штуки и запас по ТУ поставщика; предложение, пока П-1** не утверждена автором (К-5); л. 14
23	Смесь кладочная для блоков (клей или раствор — по виду изделия)	по выбору подрядчика			м³ кладки	0,56		мешок по ТУ	по ТУ		П-1**; на 0,56 м³ кладки; количество смеси — по ТУ производителя смеси (расход на м³ кладки; источника расхода в knowledge нет, число не ставится); предложение, пока П-1** не утверждена автором (К-5); л. 14
24	Перемычка над проёмом в кладке П-1**: L 1200 мм	по выбору подрядчика			шт	1		шт	1 шт		П-1**; ширина проёма + 2 × 250 мм опирания (принято, практика: СП 15 опирания не задаёт); тип перемычки — по ТУ изделия; предложение, пока П-1** не утверждена автором (К-5); л. 14
25	Кирпич керамический полнотелый на ребро: изделия кладки толщиной 120 мм	по выбору подрядчика			м³	1,30		поддон по ТУ	по ТУ		П-3**; объём кладки 10,8 м² × 120 мм; размер изделия в данных не задан штуки и запас по ТУ поставщика; предложение, пока П-3** не утверждена автором (К-5); л. 14
26	Смесь кладочная для кирпича (клей или раствор — по виду изделия)	по выбору подрядчика			м³ кладки	1,30		мешок по ТУ	по ТУ		П-3**; на 1,3 м³ кладки; количество смеси — по ТУ производителя смеси (расход на м³ кладки; источника расхода в knowledge нет, число не ставится); предложение, пока П-3** не утверждена автором (К-5); л. 14
Слаботочные сети											
27	Кабель домофона — тип по системе поставщика	по выбору подрядчика			м	6,70		бухта по ТУ	7,00 м		по лучам от ЩС**, 1 точ., запас 10 % уже в длине; 2 точ. — предложение листа слаботочки (знак «*» на плане); л. 28
28	Кабель коаксиальный RG-6 (75 Ом) к розеткам ТВ	по выбору подрядчика			м	11,70		бухта по ТУ	12,00 м		по лучам от ЩС**, 1 точ., запас 10 % уже в длине; 2 точ. — предложение листа слаботочки (знак «*» на плане); л. 28
29	Кабель U/UTP кат. 6 (LAN, Wi-Fi и камеры по PoE)	по выбору подрядчика			м	46,50		бухта по ТУ	47,00 м		по лучам от ЩС**, 5 точ., запас 10 % уже в длине; 2 точ. — предложение листа слаботочки (знак «*» на плане); л. 28
30	Гофротруба Ø20 для слаботочных линий, отдельно от силовых	по выбору подрядчика			м	58,40		бухта по ТУ	59,00 м		по длине лучей без участков в канале плинтуса (≈ 90 %); л. 28
31	Розетка компьютерная RJ45, кат. 6, с рамкой и подрозетником	по выбору подрядчика			шт	3		шт	3 шт		LAN1–LAN3; серия механизмов — как у розеток и выключателей; л. 24, 25, 28
32	Розетка телевизионная (коаксиальная) с рамкой и подрозетником	по выбору подрядчика			шт	1		шт	1 шт		ТВ1; серия механизмов — как у розеток и выключателей; л. 24, 25, 28
33	Трубка или монитор домофона (поставка домофонной организации)	по выбору подрядчика			шт	1		шт	1 шт		ДФ1; серия механизмов — как у розеток и выключателей; л. 24, 25, 28

Допущения и предложения на листе

Основа листа: размеры помещений и положение проёмов введены заказчиком в брифе, на объекте не замерены (К-1); высота потолка 2700 мм — по брифу заказчика, не замерена (К-2); толщины стен приняты по брифу: наружные 200 мм, внутренние 150 мм — не обмерены (К-1); тип дома монолитный, перекрытие 200 мм — по брифу заказчика, документов нет (К-3); планировка (стены, проёмы, объединение кухни и гостиной, расширение санузла) — по брифу без обмера и плана БТИ (К-7); разрешённая мощность 10 кВт принята, ТУ не переданы (К-8); вентканалы приняты, в брифе не заданы (К-9); подрайон климата не задан — принят не северный (жилые от 2,5 м) (К-10).

Знак «**» — предложение проектировщика, заказчиком не утверждено (согласовать с заказчиком): К-5: П-1 — положение, материал (пеноблок) и толщина 100 мм — по брифу заказчика; конструкция (кладка, армирование, штукатурка) — выбор исполнителя, автором не утверждена; кладка — не ГКЛ: каркас, листы и Rw системы не считаются (система, лист, слои, Rw — «—»); П-2 — положение, материал (ГКЛ) и толщина 150 мм — по брифу заказчика; конструкция (система С112, 2 слоя с каждой стороны, Rw 51 дБ — нижняя граница диапазона системы С112 (51–56 дБ)) — выбор исполнителя, автором не утверждена; П-3 — положение, материал (кирпич) и толщина 120 мм — по брифу заказчика; конструкция (кладка, армирование, штукатурка) — выбор исполнителя, автором не утверждена; кладка — не ГКЛ: каркас, листы и Rw системы не считаются (система, лист, слои, Rw — «—»); записи в реестре нет: ЩС — щит слаботочный: место и состав; плинтус пом. 1, 2, 5, фартук пом. 1 — артикул изделия не выбран: позиция описана характеристиками («аналог по характеристикам»), артикул выбирается при закупке.

См. лист открытых вопросов (лист 5, записи К-1–К-3, К-5, К-7–К-10).

Изм.	Кол.уч	Лист	№ док.	Подп.	Дата	ГД-2026-011-АИ			
						Квартира 56 м²			
						ЖК «Северный парк», Москва			
Разраб.		Кырлан А.С.			21.10.26	Дизайн-проект интерьера	Стадия	Лист	Листов
Пров.							РП	80	83
ГИП									
Н. контр.						Спецификация материалов (продолжение)	Кырлан Александр Сергеевич		
Утв.						М б/м			

Спецификация материалов (окончание)

Отделочные материалы: чистое количество, запас, упаковка, к заказу · ГОСТ 21.110-2013

Спецификация материалов (ГОСТ 21.110-2013, форма 1) (продолжение)

Поз.	Наименование и техническая характеристика	Тип, марка, артикул	Код продукции	Поставщик	Ед. изм.	Количество				Масса ед., кг	Примечание
						чистое	запас, %	упаковка	к заказу		
34	Щит слаботочный ЩС**: корпус, DIN-рейка, розетки 220 В	по выбору подрядчика			шт	1		шт	1 шт		ЩС**; серия механизмов — как у розеток и выключателей; л. 24, 25, 28
35	Патч-панель, портов не менее 5	по выбору подрядчика			шт	1		шт	1 шт		серия механизмов — как у розеток и выключателей; л. 24, 25, 28
Лакокрасочные материалы											
36	Краска интерьерная акриловая, матовая, класс истирания 1	Farrow & Ball Modern Emulsion No. 298 «Bancha»			л	2,60	10	банка 2,5 л	2 банк		10,82 м² × 2 сл. × 0,12 л/м²; пом. 1; л. 44
37	Краска интерьерная акриловая, матовая, класс истирания 1	Tikkurila Euro Power 7, колеровка по NCS S 0804-Y30R «S 0804-Y30R»			л	23,56	10	банка 2,7 л	10 банк		98,16 м² × 2 сл. × 0,12 л/м²; пом. 1, 2, 3, 5; л. 44
38	Краска интерьерная акриловая, глубокоматовая, класс истирания 2	Tikkurila Euro Power 7 F485 «Damask»			л	12,37	10	банка 2,7 л	6 банк		51,56 м² × 2 сл. × 0,12 л/м²; пом. 1 (пот.), 2 (пот.), 3 (пот.), 5 (пот.); л. 44
39	Краска интерьерная акриловая, матовая, класс истирания 1	Tikkurila Euro Power 7, колеровка по NCS S 5010-G70Y «S 5010-G70Y»			л	1,52	10	банка 2,7 л	1 банк		6,33 м² × 2 сл. × 0,12 л/м²; пом. 2; л. 44
40	Краска интерьерная акриловая, матовая, класс истирания 1	Tikkurila Euro Power 7 X447 «Sea Smoke»			л	1,56	10	банка 2,7 л	1 банк		6,50 м² × 2 сл. × 0,12 л/м²; пом. 3; л. 44
41	Краска интерьерная акриловая, матовая, класс истирания 1	Tikkurila Euro Power 7 F485 «Damask»			л	1,15	10	банка 2,7 л	1 банк		4,81 м² × 2 сл. × 0,12 л/м²; пом. 4 (пот.); л. 44
42	Шпаклёвка финишная полимерная под окраску (стены и потолки, Q3)	по выбору подрядчика			м²	178,18	10	ведро по ТУ	по ТУ		расход кг/м² на слой — по ТУ; л. 44
43	Грунтовка акриловая глубокого проникновения, 2 слоя	по выбору подрядчика			м²	201,80	10	канистра по ТУ	по ТУ		расход л/м² — по ТУ; л. 44
Погонажные изделия и потолки											
44	Плинтус напольный МДФ под покраску, h=80 мм, крепление к стене	аналог: плинтус МДФ под покраску 80×16			м.п.	38,90	10	хлыст 2,4 м	18 шт		пом. 1, 2, 5; длина хлыста — по артикулу; л. 44
45	Плинтус напольный МДФ под покраску, h=69 мм, крепление к стене	SX165			м.п.	11,00	10	хлыст 2,4 м	6 шт		пом. 3; длина хлыста — по артикулу; л. 44
46	Потолок подвесной ГКЛ/ГКЛВ по каркасу Knauf П113: листы, профили, подвесы, лента, шпаклёвка швов	Knauf П113			м²	56,37		комплект	по л. потолков		площадь — по ведомости потолков; число листов, профилей и подвесов — по шагам каркаса на листе потолков; л. 36–39

Примечания

1. Чистое количество — из ведомости объёмов работ и раскладки плитки; запас — отдельной графой (доска — по ведомости отделки, плитка, краска и плинтус — 10 %); «к заказу» — с запасом и кратно упаковке.
2. Плитка — штуками по раскладке, запас на каждую поверхность. Калибр (рабочий размер) и тон — одной партией на помещение, калибр указать при заказе и сверить с раскладкой до укладки.
3. Краска — 0,12 л/м² на слой (середина вилки 0,10–0,15 л/м²) по фактической площади окраски из ведомости отделки; колеровка одной партией.
4. «По ТУ» — расход задаёт производитель выбранного продукта; количество к заказу — после выбора марки.
5. Поз. 3, 4, 6, 44 заданы характеристиками («аналог:»): марку, артикул и поставщика согласовать с заказчиком до закупки, без артикула не заказывать.
6. Штукатурная смесь — на ту же площадь, что строка ВОР «Штукатурка стен» (134,75 м²): площадь одна, расход смеси задаёт производитель.
7. Коробы инсталляции и стояков: ГКЛВ в 2 слоя и профиль 27 × 28 мм считаются по свободным граням коробов (источник — раскладка плиточника и шахты в данных); короб К1 над полом — в спецификации ВК.
8. Потолки ГКЛ: в этой спецификации — площадь системы П113; число листов, профилей и подвесов — по шагам каркаса на листе потолков (подвесы через 1000, несущие через 500, основные через 1200 мм), схема каркаса не выпущена. Сантехника, светильники и мебель — по своим спецификациям.

Допущения и предложения на листе

Основа листа: размеры помещений и положение проёмов введены заказчиком в брифе, на объекте не замерены (К-1); высота потолка 2700 мм — по брифу заказчика, не замерена (К-2); толщины стен приняты по брифу: наружные 200 мм, внутренние 150 мм — не обмерены (К-1); тип дома монолитный, перекрытие 200 мм — по брифу заказчика, документов нет (К-3); планировка (стены, проёмы, объединение кухни и гостиной, расширение санузла) — по брифу без обмера и плана БТИ (К-7); разрешённая мощность 10 кВт принята, ТУ не переданы (К-8); вентканалы приняты, в брифе не заданы (К-9); подрайон климата не задан — принят не северный (жилые от 2,5 м) (К-10).

Знак «**» — предложение проектировщика, заказчиком не утверждено (согласовать с заказчиком): записи в реестре нет: ЩС — щит слаботочный: место и состав; плинтус пом. 1, 2, 5, фартук пом. 1 — артикул изделия не выбран: позиция описана характеристиками («аналог по характеристикам»), артикул выбирается при закупке.

См. лист открытых вопросов (лист 5, записи К-1–К-3, К-7–К-10).

Изм.	Кол.уч	Лист	№ док.	Подп.	Дата	ГД-2026-011-АИ			
						Квартира 56 м²			
						ЖК «Северный парк», Москва			
Разраб.		Кырлан А.С.			21.10.26	Дизайн-проект интерьера	Стадия	Лист	Листов
Пров.							РП	81	83
ГИП									
Н. контр.						Спецификация материалов (окончание) М б/м	Кырлан Александр Сергеевич		
Утв.									

выпуск 19.10.2026 № 1c3e34763b · стр. 93 из 117

Смета ориентировочная

ПРЕДВАРИТЕЛЬНО · не для производства работ · открыто пунктов: 10 (реестр — л. 5)

Работы, материалы, оборудование, услуги и резерв · цены — ориентир по открытым прайсам, не коммерческое предложение

Сводная смета (прайсы собраны 21.09.2026, часть расценок сверена повторно 06.10.2026, Москва)

№	Наименование работ, материалов, услуг	Ед. изм.	Кол-во	Цена за ед., ₽	Стоимость, ₽			Чей подряд	Срок поставки, дн.	Основание	Источник цены
					план	факт	разница				
Работы — по ведомости объёмов работ											
1	Демонтаж и черновые работы (без 9 поз. по КП)	раздел	1		206 611			бригада		ВОР, поз. 1–15; л. 76–78	по ВОР
2	Инженерные системы (без 11 поз. по КП)	раздел	1		148 108			бригада		ВОР, поз. 16–37; л. 76–78	по ВОР
3	Чистовые работы (без 1 поз. по КП)	раздел	1		429 853			бригада, поставщик		ВОР, поз. 38–55; л. 76–78	по ВОР
Материалы — по спецификации материалов											
4	Инженерная доска	м²	46,20	4 513	208 501			поставщик		спецификация, поз. 1	Ц7
5	Керамогранит 600×600 мм	м²	6,12	1 800	11 016			поставщик		спецификация, поз. 3	Ц6
6	Керамогранит 600×1200, 1200×600 мм	м²	49,68	3 500	173 880			поставщик		спецификация, поз. 4, 5, 6	Ц6
7	Клей плиточный цементный класса C2 TE S1	меш.	12	1 800	21 600			поставщик		спецификация, поз. 7	Ц7
8	Затирка цементная класса CG2WA	упак.	2	1 000	2 000			поставщик		спецификация, поз. 8	Ц7
9	Краска Farrow & Ball Modern Emulsion, банка 2,5 л	банк	2	5 800	11 600			поставщик		спецификация, поз. 36	Ц7
10	Краска Tikkurila (Euro Power 7, колеровка по NCS, Euro Power 7), банка 2,7 л	банк	19	3 510	66 690			поставщик		спецификация, поз. 37, 38, 39, 40, 41	Ц6
11	Плинтус напольный МДФ под покраску	шт	24	368	8 832			поставщик		спецификация, поз. 44, 45	Ц7
12	Прочие материалы с расходом по ТУ (клей для доски, гидроизоляция, демпферная лента, смесь для стяжки, смесь штукатурная гипсовая для машинного и ручного нанесения по маякам, лист гклв 12, профиль стальной оцинкованный 27 × 28 мм: каркас коробов (стойки и направляющие), ГКЛВ перегородок, профиль ПН, профиль ПС, профиль УА, минвата в каркас, лента уплотнительная, крепёж каркаса, изделия кладки, кладочная смесь, перемычки, кабель слаботочки, гофра слаботочки, изделия слаботочки, шпаклёвка, грунтовка, каркас и ГКЛ потолков)	компл	1	по КП				поставщик		спецификация, поз. 2, 9, 10, 11, 12, 13, 14, 15, 16, 17, 18, 19, 20, 21, 22, 23, 24, 25, 26, 27, 28, 29, 30, 31, 32, 33, 34, 35, 42, 43, 46	
Оборудование и мебель — поставка по спецификациям											
13	Кухонный гарнитур по проекту кухни, изготовление и монтаж (4–8 нед.)	компл	1	по КП				поставщик	уточн.; ориентир 4–8 нед. от замера	л. 57, 58	
14	Двери скрытого монтажа с коробом под покраску, поставка	шт	4	по КП				поставщик	уточн.; ориентир ≈ 30 дн.	л. 15	

Допущения и предложения на листе

Основа листа: размеры помещений и положение проёмов введены заказчиком в брифе, на объекте не замерены (К-1); высота потолка 2700 мм — по брифу заказчика, не замерена (К-2); толщины стен приняты по брифу: наружные 200 мм, внутренние 150 мм — не обмерены (К-1); тип дома монолитный, перекрытие 200 мм — по брифу заказчика, документов нет (К-3); планировка (стены, проёмы, объединение кухни и гостиной, расширение санузла) — по брифу без обмера и плана БТИ (К-7); разрешённая мощность 10 кВт принята, ТУ не переданы (К-8); вентканалы приняты, в брифе не заданы (К-9); подрайон климата не задан — принят не северный (жилые от 2,5 м) (К-10).

См. лист открытых вопросов (лист 5, записи К-1–К-3, К-7–К-10).

Изм.	Кол.уч	Лист	№ док.	Подп.	Дата
Разраб.		Кырлан А.С.			21.10.26
Пров.					
ГИП					
Н. контр.					
Утв.					

ГД-2026-011-АИ

Квартира 56 м²

ЖК «Северный парк», Москва

Дизайн-проект интерьера

Стадия	Лист	Листов
РП	82	83

Смета ориентировочная

М б/м

Кырлан Александр Сергеевич

Смета ориентировочная (окончание)

ПРЕДВАРИТЕЛЬНО · не для производства работ · открыто пунктов: 10 (реестр — л. 5)

Работы, материалы, оборудование, услуги и резерв · цены — ориентир по открытым прайсам, не коммерческое предложение

Сводная смета (прайсы собраны 21.09.2026, часть расценок сверена повторно 06.10.2026, Москва) (продолжение)

№	Наименование работ, материалов, услуг	Ед. изм.	Кол-во	Цена за ед., ₽	Стоимость, ₽			Чей подряд	Срок поставки, дн.	Основание	Источник цены
					план	факт	разница				
15	Оборудование заказчика слаботочных сетей: точка доступа wi-fi — 2 шт; коммутатор — 1 шт	компл	1	по КП				заказчик		л. 24, 25	
16	Сантехника, светильники, мебель и предметы интерьера	компл	1	по КП				поставщик		л. 33; л. 34; л. 60; л. 18–20	
Прочие работы и услуги											
17	Вынос и вывоз строительного мусора	м³		по факту				бригада		после демонтажа	
18	Подъём материалов на этаж (лифтом или вручную — по договору)	т		по факту				бригада		по массе поставки	
19	Доставка чистовых материалов, 10 % от поставки			10 %	50 412			поставщик		от суммы материалов	
20	Уборка после ремонта	м²	56,37	по факту				бригада		S квартиры	
	Итого работы				**784 572**						
	Итого материалы				**504 119**						
	Итого прочие услуги				**50 412**						
	Резерв на непредвиденные работы и материалы, 15 %				**200 865**						
	ВСЕГО ориентировочно (без оборудования и позиций по КП)				**1 539 968**						

Примечания

1. Смета ориентировочная, не коммерческое предложение: объёмы — из ведомости объёмов работ и спецификации материалов, цены — нижняя граница открытых прайсов Москвы (прайсы собраны 21.09.2026, часть расценок сверена повторно 06.10.2026); перед договором цены подтвердить у подрядчика и поставщиков.
2. Источники цен: Ц1 — Домашний мастерок: прайс на отделочные работы, 2026; Ц2 — Домашний мастерок: прайс на плиточные работы, 2026; Ц3 Домашний мастерок: прайс на электромонтажные работы, 2026; Ц4 — Профи ремонтник: штукатурно-малярные работы; Ц5 — Profi.ru: укладка керамогранита на стены, Москва 2026; Ц6 — knowledge/spec-materials.md, разд. 1 и 3: ориентир по сегментам; Ц7 — Розница Москвы, 09.2026: Леманa ПРО, KGSnab, официальный дилер Farrow & Ball.
3. Повторная сверка с прайсом: 06.10.2026 — перегородка в 2 слоя с усиленным каркасом; остальные расценки — по прайсам, собранным 21.09.2026.
4. В итог не вошли позиции «по КП» и «по факту»: оборудование и мебель, двери, материалы с расходом по ТУ, вывоз мусора, подъём и уборка.
5. В разделе 1 учтены работы по П-2** — 14 418 ₽ (расценка Ц1 за м² конструкции; П-2** — по расценке «усиленный каркас» 2 700 ₽/м² вместо 1 500 ₽/м²: шаг стоек 400 мм или проём с обрамлением УА): это предложение проектировщика, не утверждённое автором (К-5); если конструкции не будет, строки и материалы к ним снимаются, санузел 2 пересчитывается. Обрамление проёма УА, заполнение, профиль и обшивка — материалы «по ТУ», в итог не входят.
6. Доставка — 10 % от материалов, резерв — 15 % (частный ремонт 10–20 %) отдельными строками, в количествах не спрятаны. Графы «факт» и «разница» заполняются по актам.

Допущения и предложения на листе

Основа листа: размеры помещений и положение проёмов введены заказчиком в брифе, на объекте не замерены (К-1); высота потолка 2700 мм — по брифу заказчика, не замерена (К-2); толщины стен приняты по брифу: наружные 200 мм, внутренние 150 мм — не обмерены (К-1); тип дома монолитный, перекрытие 200 мм — по брифу заказчика, документов нет (К-3); планировка (стены, проёмы, объединение кухни и гостиной, расширение санузла) — по брифу без обмера и плана БТИ (К-7); разрешённая мощность 10 кВт принята, ТУ не переданы (К-8); вентканалы приняты, в брифе не заданы (К-9); подрайон климата не задан — принят не северный (жилые от 2,5 м) (К-10).

Знак «**» — предложение проектировщика, заказчиком не утверждено (согласовать с заказчиком): К-5: П-2 — положение, материал (ГКЛ) и толщина 150 мм — по брифу заказчика; конструкция (система С112, 2 слоя с каждой стороны, Rw 51 дБ — нижняя граница диапазона системы С112 (51–56 дБ)) — выбор исполнителя, автором не утверждена.

См. лист открытых вопросов (лист 5, записи К-1–К-3, К-5, К-7–К-10).

						ГД-2026-011-АИ	
						Квартира 56 м²	
						ЖК «Северный парк», Москва	
Изм.	Кол.уч	Лист	№ док.	Подп.	Дата		
Разраб.		Кырлан А.С.			21.10.26	Дизайн-проект интерьера	Стадия: РП; Лист: 83; Листов: 83
Пров.							
ГИП							
						Смета ориентировочная (окончание)	**Кырлан Александр Сергеевич**
Н. контр.						М б/м	
Утв.							

выпуск 19.10.2026 № 1c3e34763b · стр. 95 из 117

11

Визуализации

Кырлан Александр Сергеевич

выпуск 19.10.2026 № 1c3e34763b · стр. 96 из 117



Планировочное решение · вид сверху

Квартира 56 м² · визуализация 1 из 21

выпуск 19.10.2026 № 1c3e34763b · стр. 97 из 117



room-bath-wA

Квартира 56 м² · визуализация 2 из 21

выпуск 19.10.2026 № 1c3e34763b · стр. 98 из 117



room-bath-wB

Квартира 56 м² · визуализация 3 из 21

выпуск 19.10.2026 № 1c3e34763b · стр. 99 из 117



room-bath-wC

Квартира 56 м² · визуализация 4 из 21

выпуск 19.10.2026 № 1c3e34763b · стр. 100 из 117



room-bath-wD

Квартира 56 м² · визуализация 5 из 21

выпуск 19.10.2026 № 1c3e34763b · стр. 101 из 117

выпуск 19.10.2026 № 1c3e34763b · стр. 102 из 117



room-bedroom-wA

выпуск 19.10.2026 № 1c3e34763b · стр. 103 из 117



room-bedroom-wB



room-bedroom-wC

Квартира 56 м² · визуализация 8 из 21

выпуск 19.10.2026 № 1c3e34763b · стр. 104 из 117



room-bedroom-wD

Квартира 56 м² · визуализация 9 из 21

выпуск 19.10.2026 № 1c3e34763b · стр. 105 из 117



room-hall-wA

Квартира 56 м² · визуализация 10 из 21

выпуск 19.10.2026 № 1c3e34763b · стр. 106 из 117



room-hall-wB

Квартира 56 м² · визуализация 11 из 21

выпуск 19.10.2026 № 1c3e34763b · стр. 107 из 117

выпуск 19.10.2026 № 1c3e34763b · стр. 108 из 117

room-hall-wC



room-hall-wD

Квартира 56 м² · визуализация 13 из 21

выпуск 19.10.2026 № 1c3e34763b · стр. 109 из 117



room-kids-wA

Квартира 56 м² · визуализация 14 из 21

выпуск 19.10.2026 № 1c3e34763b · стр. 110 из 117



room-kids-wB

Квартира 56 м² · визуализация 15 из 21

выпуск 19.10.2026 № 1c3e34763b · стр. 111 из 117



room-kids-wC

Квартира 56 м² · визуализация 16 из 21

выпуск 19.10.2026 № 1c3e34763b · стр. 112 из 117



room-kids-wD

Квартира 56 м² · визуализация 17 из 21



room-living-wA

Квартира 56 м² · визуализация 18 из 21

выпуск 19.10.2026 № 1c3e347763b · стр. 114 из 117



room-living-wB

Квартира 56 м² · визуализация 19 из 21

выпуск 19.10.2026 № 1c3e34763b · стр. 115 из 117



room-living-wC

Квартира 56 м² · визуализация 20 из 21

выпуск 19.10.2026 № 1c3e34763b · стр. 116 из 117



room-living-wD

Квартира 56 м² · визуализация 21 из 21

выпуск 19.10.2026 № 1c3e34763b · стр. 117 из 117